LINEA

РАБОЧАЯ ДОКУМЕНТАЦИЯ

Четырёхкомнатная квартира

13 помещений

Шифр комплекта ГД-2026-004-АИ

Стадия РП

Дата выпуска 05.10.2026

ПРЕДВАРИТЕЛЬНО · не для производства работ
открыто пунктов: 30 (реестр — л. 6–11)

ДИЗАЙНЕР

Кырлан Александр Сергеевич

Содержание

ПРЕДВАРИТЕЛЬНО · не для производства работ · открыто пунктов: 30 (реестр — л. 6–11)

03 Общие данные 19 л.

22 Архитектурные решения 3 л.

26 Планировочное решение 6 л.

33 Электрооборудование 9 л.

43 Отопление и вентиляция 2 л.

46 Водоснабжение и канализация 4 л.

51 Потолки и ГКЛ-конструкции 9 л.

61 Полы и отделка 11 л.

73 Декор и текстиль 25 л.

99 Развёртки и узлы 29 л.

129 Смета 7 л.

137 Визуализации 31 л.

ДИЗАЙН-ПРОЕКТ ИНТЕРЬЕРА

Четырёхкомнатная квартира

13 помещений

102,67 м²

актуальность · комфорт · мягкая геометрия · контраст фактур · открытость · уверенность

60 % — тёплый белый Paper F497 и песочный Castle J484, 30 % — грейж Claystone V486 в фасадах встроенного хранения и текстиле, 10 % — коричнево-лиловый Silhouette L481 из палитры стиля: ТВ-стена зала, изголовья детских, фасад кухонного острова. По практике тёплая аналоговая гамма ровнее держит цвет в квартире с окнами на разные стороны.

ПАЛИТРА 60 / 30 / 10

F497	J484	V486	L481
60 %	60 %	30 %	10 %

АВТОР ПРОЕКТА

Кырлан Александр Сергеевич

Октябрь 2026

Визуализация 1 · Вид сверху (3D): планировка с мебелью, текстилем и декором

ОБЪЕКТ	ОБЩАЯ ПЛОЩАДЬ	ПОМЕЩЕНИЙ
Четырёхкомнатная квартира	102,67 м²	13, из них жилых 4
СТИЛЬ	**СТАДИЯ**	**ШИФР**
Современный (контемпорари) · 13 помещений	Рабочий проект · предварительно	ГД-2026-004-АИ

Изм.	Кол.уч	Лист	№ док.	Подп.	Дата			
Разраб.		Кырлан А.С.			21.10.26	ГД-2026-004-АИ		
Пров.						Четырёхкомнатная квартира Общая площадь 102,67* м² · * размеры со скана, не замерены (реестр — л. 6–11, ИЗ-8, К-20, К-21)		
ГИП		Кырлан А.С.			21.10.26	Дизайн-проект интерьера четырёхкомнатной квартиры	Стадия: РП	Лист: 1 / Листов: 124
Н. контр.						**Титульный лист** М б/м	**Кырлан Александр Сергеевич**	
Утв.								

выпуск 05.10.2026 № 7e7a2cd217 · стр. 3 из 168

Общие данные

Комплект ГД-2026-004-АИ · Квартира с эркерами · 13 помещений

ПРЕДВАРИТЕЛЬНО · не для производства работ · открыто пунктов: 30 (реестр — л. 6–11)

Ведомость рабочих чертежей основного комплекта ГД-2026-004-АИ

Лист	Наименование	Примечание
1	Титульный лист	
2	Общие данные	
3	Общие данные	
4	Общие данные	
5	Общие данные	
6	Открытые вопросы, принятые допущения и конфликты. Лист 1 из 6	
7	Открытые вопросы, принятые допущения и конфликты. Лист 2 из 6	
8	Открытые вопросы, принятые допущения и конфликты. Лист 3 из 6	
9	Открытые вопросы, принятые допущения и конфликты. Лист 4 из 6	
10	Открытые вопросы, принятые допущения и конфликты. Лист 5 из 6	
11	Открытые вопросы, принятые допущения и конфликты. Лист 6 из 6	
12	Задание на контрольный обмер и обследование. Лист 1 из 5	
13	Задание на контрольный обмер и обследование. Лист 2 из 5	
14	Задание на контрольный обмер и обследование. Лист 3 из 5	
15	Задание на контрольный обмер и обследование. Лист 4 из 5	
16	Задание на контрольный обмер и обследование. Лист 5 из 5	
17	График закупок и работ. Лист 1 из 3	
18	График закупок и работ. Лист 2 из 3	
19	График закупок и работ. Лист 3 из 3	
20	Обмерный план	
21	План демонтажа и монтажа перегородок	
22	План дверей и ведомость заполнения проёмов	
23	Концепция интерьера	
24	План расстановки мебели	
25	Спецификация мебели и оборудования	
26	Спецификация мебели и оборудования (продолжение)	
27	Спецификация мебели и оборудования (продолжение)	
28	Спецификация мебели и оборудования (продолжение)	
29	План розеток и электровыводов	
30	План освещения	Допущения и предложения на листе. См. лист открытых вопросов (листы 6–11).

Общие указания — лист 5: ±0,000 — чистый пол; несущие конструкции и сети дома — по отдельному проекту; скрытые работы — по актам. Открытые вопросы и допущения — листы 6–11.

Ведомость рабочих чертежей основного комплекта ГД-2026-004-АИ (продолжение)

Лист	Наименование	Примечание
31	План выключателей и схема включения	
32	Ведомость электроточек и изделий	
33	Ведомость электроточек и изделий (продолжение)	
34	Однолинейная схема щита	
35	Однолинейная схема щита (продолжение)	
36	План принципиальных трасс	
37	План слаботочных сетей	
38	План вентиляции	
39	План отопления	
40	План выводов сантехники	
41	Схема разводки водопровода и канализации	
42	Спецификация сантехнического оборудования	
43	Спецификация светильников и сценарии освещения	
44	План потолков	
45	Разрезы и узлы потолков	
46	Разрезы и узлы потолков (продолжение)	
47	Разрезы и узлы потолков (продолжение)	
48	Разрезы и узлы потолков (продолжение)	
49	Раскладка плитки. Планы полов	
50	Раскладка плитки. Фартук кухни	
51	Раскладка плитки. Ванная комната. Развёртки стен	
52	Раскладка плитки. Санузел. Развёртки стен	
53	План полов	

Изм.	Кол.уч	Лист	№ док.	Подп.	Дата	ГД-2026-004-АИ		
						Четырёхкомнатная квартира		
						Общая площадь 102,67* м² · * размеры со скана, не замерены (реестр — л. 6–11, ИЗ-8, К-20, К-21)		
Разраб.		Кырлан А.С.			21.10.26	Дизайн-проект интерьера четырёхкомнатной квартиры	Стадия: РП	Лист: 2 / Листов: 124
Пров.								
ГИП		Кырлан А.С.			21.10.26			
Н. контр.						Общие данные	Кырлан Александр Сергеевич	
Утв.						М б/м		

выпуск 05.10.2026 № 7e7a2cd217 · стр. 4 из 168

Общие данные

Комплект ГД-2026-004-АИ · лист 2 общих данных (продолжение)

Ведомость рабочих чертежей основного комплекта ГД-2026-004-АИ (продолжение)

Лист	Наименование	Примечание
54	Конструкции полов и стыки покрытий	
55	Ведомость отделки помещений. Лист 1 из 3	
56	Ведомость отделки помещений. Лист 2 из 3	
57	Ведомость отделки помещений. Лист 3 из 3	
58	Колерная карта	
59	Колерная карта	
60	Спецификация отделочных материалов	
61	Спецификация отделочных материалов	
62	Концепция декора и визуализации	
63	План текстиля и декора	
64	Шторы и карнизы	
65	Ведомость текстиля	
66	Ведомость декора. Схемы развески	
67	Встроенная мебель. Схема расположения	
68	Система хранения М8	
69	Система хранения М9	
70	Система хранения М10	
71	Шкаф распашной М16	
72	Система хранения М18	
73	Система хранения М19	
74	Шкаф-купе М29	
75	Система хранения М32	
76	Система хранения М33	
77	Шкаф распашной М35	
78	Система хранения М39	
79	Система хранения М41	
80	Система хранения М42	Допущения и предложения на листе. См. лист открытых вопросов (листы 6–11).
81	Кухня (пом. 6). Развёртка гарнитура	
82	Кухня (пом. 6). Монтажная схема	
83	Кухня (пом. 6). Развёртка гарнитура	

Ведомость рабочих чертежей основного комплекта ГД-2026-004-АИ (продолжение)

Лист	Наименование	Примечание
84	Кухня (пом. 6). Монтажная схема	
85	Шкафы. Монтажная схема. Лист 1 из 3	
86	Шкафы. Монтажная схема. Лист 2 из 3	
87	Шкафы. Монтажная схема. Лист 3 из 3	
88	Ведомости изделий, техники и фурнитуры	
89	Реестр марок отделки и позиций альбома	
90	Схема расположения развёрток и узлов	
91	Развёртки стен А, Б. Зал (пом. 1)	
92	Развёртки стен В, Г. Зал (пом. 1)	
93	Развёртка стены А. Ванная комната (пом. 2)	
94	Развёртка стены Б. Ванная комната (пом. 2)	
95	Развёртка стены В. Ванная комната (пом. 2)	
96	Развёртка стены Г. Ванная комната (пом. 2)	
97	Развёртки стен. Тёмная комната (пом. 3)	
98	Развёртки стен А, Б. Детская 1 (пом. 4)	
99	Развёртки стен В, Г. Детская 1 (пом. 4)	
100	Развёртки стен А, Б. Коридор (пом. 5)	
101	Развёртка стены В. Коридор (пом. 5)	
102	Развёртка стены А. Кухня (пом. 6), кухонный фронт	
103	Развёртки стен Б, В. Кухня (пом. 6)	
104	Развёртка стены Г. Кухня (пом. 6)	
105	Развёртки стен А, Б, В. Прихожая-коридор (пом. 7)	
106	Развёртка стены Г. Прихожая-коридор (пом. 7)	

Общие указания — лист 5: ±0,000 — чистый пол; несущие конструкции и сети дома — по отдельному проекту; скрытые работы — по актам. Открытые вопросы и допущения — листы 6–11.

Изм.	Кол.уч	Лист	№ док.	Подп.	Дата	ГД-2026-004-АИ		
						Четырёхкомнатная квартира		
						Общая площадь 102,67* м² · * размеры со скана, не замерены (реестр — л. 6–11, ИЗ-8, К-20, К-21)		
Разраб.		Кырлан А.С.			21.10.26	Дизайн-проект интерьера четырёхкомнатной квартиры	Стадия	Лист	Листов
Пров.							РП	3	124
ГИП		Кырлан А.С.			21.10.26				
						Общие данные	**Кырлан Александр Сергеевич**		
Н. контр.						М б/м			
Утв.									

выпуск 05.10.2026 № 7e7a2cd217 · стр. 5 из 168

Общие данные

Комплект ГД-2026-004-АИ · лист 3 общих данных (продолжение)

Допущения и предложения на листе. См. лист открытых вопросов (листы 6–11).

Ведомость рабочих чертежей основного комплекта ГД-2026-004-АИ (продолжение)

Лист	Наименование	Примечание
107	Развёртки стен. Гардеробная 2 (пом. 8)	
108	Развёртки стен А, Б. Детская 2 (пом. 9)	
109	Развёртки стен В, Г. Детская 2 (пом. 9)	
110	Развёртки стен А, Б. Санузел (пом. 10)	
111	Развёртки стен В, Г. Санузел (пом. 10)	
112	Развёртки стен А, Б. Гостиная (пом. 11)	
113	Развёртки стен В, Г. Гостиная (пом. 11)	
114	Развёртки стен. Гардеробная 1 (пом. 12)	
115	Развёртки стен А, Б, В. Балкон 1 (пом. 13)	
116	Развёртка стены Г. Балкон 1 (пом. 13)	
117	Узлы	
118	Ведомость объёмов работ	
119	Ведомость объёмов работ (продолжение)	
120	Ведомость объёмов работ (окончание)	
121	Спецификация материалов	
122	Спецификация материалов (окончание)	
123	Смета ориентировочная	
124	Смета ориентировочная (окончание)	

Ведомость ссылочных и прилагаемых документов

Обозначение	Наименование	Примечание
	Ссылочные документы	
ГОСТ 21.201-2011	СПДС. Условные графические изображения элементов зданий, сооружений и конструкций	
ГОСТ 21.205-2016	СПДС. Условные обозначения элементов санитарно-технических систем	
ГОСТ 21.210-2014	СПДС. Изображения условные графические электрооборудования и проводок на планах	
ГОСТ 2.306-68	ЕСКД. Обозначения графические материалов и правила их нанесения на чертежах	
	Прилагаемые документы	
ГД-2026-004-АИ.В1	Визуализация. Вид сверху (3D): планировка с мебелью, текстилем и декором	альбом визуализаций

Ведомость ссылочных и прилагаемых документов (продолжение)

Обозначение	Наименование	Примечание
ГД-2026-004-АИ.В2	Визуализация. Потолок	
ГД-2026-004-АИ.В3	Визуализация. Потолок: Ванная комната (пом. 2)	
ГД-2026-004-АИ.В4	Визуализация. Потолок: Прихожая-коридор (пом. 7)	
ГД-2026-004-АИ.В5	Визуализация. Потолок: Детская 1 (пом. 4)	
ГД-2026-004-АИ.В6	Визуализация. Потолок: Детская 2 (пом. 9)	
ГД-2026-004-АИ.В7	Визуализация. Потолок: Кухня (пом. 6)	
ГД-2026-004-АИ.В8	Визуализация. Потолок: Зал (пом. 1)	
ГД-2026-004-АИ.В9	Визуализация. Потолок	
ГД-2026-004-АИ.В10	Визуализация. Потолок: Гардеробная 2 (пом. 8)	
ГД-2026-004-АИ.В11	Визуализация. Потолок: Санузел (пом. 10)	
ГД-2026-004-АИ.В12	Визуализация. Визуализация «room-balcony-wD»	
ГД-2026-004-АИ.В13	Визуализация. Визуализация «room-bath-wB»	
ГД-2026-004-АИ.В14	Визуализация. Визуализация «room-corridor-wA»	
ГД-2026-004-АИ.В15	Визуализация. Визуализация «room-corridor-wC»	
ГД-2026-004-АИ.В16	Визуализация. Визуализация «room-hall-wide»	
ГД-2026-004-АИ.В17	Визуализация. Визуализация «room-kids1-wC»	
ГД-2026-004-АИ.В18	Визуализация. Визуализация «room-kids1-wD»	
ГД-2026-004-АИ.В19	Визуализация. Визуализация «room-kids2-wA»	
ГД-2026-004-АИ.В20	Визуализация. Визуализация «room-kids2-wD»	
ГД-2026-004-АИ.В21	Визуализация. Визуализация «room-kitchen-wA»	
ГД-2026-004-АИ.В22	Визуализация. Визуализация «room-living1-wA»	
ГД-2026-004-АИ.В23	Визуализация. Визуализация «room-living1-wB»	
ГД-2026-004-АИ.В24	Визуализация. Визуализация «room-living1-wC»	

Общие указания — лист 5: ±0,000 — чистый пол; несущие конструкции и сети дома — по отдельному проекту; скрытые работы — по актам. Открытые вопросы и допущения — листы 6–11.

Изм.	Кол.уч	Лист	№ док.	Подп.	Дата	ГД-2026-004-АИ		
						Четырёхкомнатная квартира		
						Общая площадь 102,67* м² · * размеры со скана, не замерены (реестр — л. 6–11, ИЗ-8, К-20, К-21)		
Разраб.		Кырлан А.С.			21.10.26	Дизайн-проект интерьера четырёхкомнатной квартиры	Стадия	Лист	Листов
Пров.							РП	4	124
ГИП		Кырлан А.С.			21.10.26				
						Общие данные	**Кырлан Александр Сергеевич**		
Н. контр.						М б/м			
Утв.									

выпуск 05.10.2026 № 7e7a2cd217 · стр. 6 из 168

Общие данные

Комплект ГД-2026-004-АИ · лист 4 общих данных (продолжение)

Ведомость ссылочных и прилагаемых документов (продолжение)

Обозначение	Наименование	Примечание
ГД-2026-004-АИ.В25	Визуализация. Визуализация «room-living1-wD»	
ГД-2026-004-АИ.В26	Визуализация. Визуализация «room-living2-wA»	
ГД-2026-004-АИ.В27	Визуализация. Визуализация «room-living2-wB»	
ГД-2026-004-АИ.В28	Визуализация. Визуализация «room-storage-wide»	
ГД-2026-004-АИ.В29	Визуализация. Визуализация «room-wardrobe1-wide»	
ГД-2026-004-АИ.В30	Визуализация. Визуализация «room-wardrobe2-wide»	
ГД-2026-004-АИ.В31	Визуализация. Визуализация «room-wc-wide»	

Состав дизайн-проекта

Раздел	Состав	Листы
Обложка	Дизайн-проект интерьера четырёхкомнатной квартиры; Четырёхкомнатная квартира; автор проекта — Кырлан Александр Сергеевич	1 с.
Концепция	Стиль Современный (контемпорари): концепция интерьера, палитра и материалы (колерная карта — лист 58)	л. 23
Визуализации	31 изобр.: Вид сверху (3D): планировка с мебелью, текстилем и декором; Потолок; Потолок: Ванная комната; Потолок: Прихожая-коридор; Потолок: Детская 1; Потолок: Детская 2; Потолок: Кухня; Потолок: Зал; Потолок; Потолок: Гардеробная 2; Потолок: Санузел; Визуализация «room-balcony-wD»; Визуализация «room-bath-wB»; Визуализация «room-corridor-wA»; Визуализация «room-corridor-wC»; Визуализация «room-hall-wide»; Визуализация «room-kids1-wC»; Визуализация «room-kids1-wD»; Визуализация «room-kids2-wA»; Визуализация «room-kids2-wD»; Визуализация «room-kitchen-wA»; Визуализация «room-living1-wA»; Визуализация «room-living1-wB»; Визуализация «room-living1-wC»; Визуализация «room-living1-wD»; Визуализация «room-living2-wA»; Визуализация «room-living2-wB»; Визуализация «room-storage-wide»; Визуализация «room-wardrobe1-wide»; Визуализация «room-wardrobe2-wide»; Визуализация «room-wc-wide»	В1–В31
Рабочие чертежи	планы, развёртки, узлы (развёртки и узлы — листы 90–92, 97–100, 103, 105, 107–115, 117)	л. 1–124
Спецификации и ведомости	оборудование, изделия, отделка, электроточки	л. 22, 25–28, 32, 33, 42, 43, 55–61, 65, 66, 118–122

Условные обозначения

- контрольный отрезок 1000 мм натуры: по нему проверяют печать 1:1
- отметка уровня, м: ±0,000 — чистый пол жилых помещений
- А — марка развёртки: буква стены, стрелка — взгляд
- О1 — марка отделки по реестру отделки альбома
- выноска узла: над полкой — узел, под полкой — лист

Допущения и предложения на листе

Основа листа: размеры сняты с размерных цепочек растрового скана плана заказчика, на объекте не замерены; ступени наружного контура приведены к граням помещений модели (ИЗ-8, К-20, К-21); высота потолка 2700 мм принята, источника нет (К-24); тип дома и перекрытие (монолит, плита 220 мм) приняты, источника нет (К-3); толщины стен приняты (250 и 120 мм), источника нет (К-21); мощность 15 кВт принята, технических условий нет (К-25).

См. лист открытых вопросов (лист 6, запись К-3; лист 7, записи К-20, К-21, К-24, К-25; лист 10, запись ИЗ-8).

Общие указания

1. Рабочие чертежи интерьера разработаны на основании задания на проектирование и обмерного плана (лист 20). Объект: Четырёхкомнатная квартира; автор проекта — Кырлан Александр Сергеевич; общая площадь 102,67 м², жилая 61,18 м², помещений 12.
2. Рабочие чертежи выполнены в соответствии с заданием на проектирование и нормативными документами, перечисленными в п. 4.
3. Открытые вопросы, принятые допущения и конфликты между разделами, не снятые к выпуску комплекта, сведены в таблицы на листах 6–11. До ответа по пункту таблицы показанное на указанном там листе — допущение, а не утверждённое решение: комплект по этим листам предварительный.
4. Нормативные документы, на которые есть ссылки в листах комплекта: ГОСТ Р 21.101-2026; ГОСТ 21.501-2018; ГОСТ 2.302-68; ГОСТ 2.303-68; ГОСТ 2.304-81; ГОСТ 2.307-2011; СП 54.13330.2022; СП 71.13330.2017; СП 73.13330.2016; ПУЭ (7-е изд.), гл. 1.8, 7.1; ГОСТ Р 50571.7.701-2024; СанПиН 1.2.3685-21; ГОСТ 2.702; ГОСТ 2.755; ГОСТ 21.110-2013; ГОСТ 21.601; ГОСТ 475-2016; ГОСТ 23166-2021; ГОСТ 31565-2012; ГОСТ 31975; ГОСТ 32414-2013; ГОСТ 32415-2013; ГОСТ Р 56387-2018; СП 29.13330.2011; СП 30.13330.2020; СП 51.13330.2011; СП 52.13330.2016. Документы из ведомости ссылочных документов здесь не повторяются.
5. За отметку ±0,000 принят уровень чистого пола жилых помещений квартиры (относительная отметка; абсолютная — по проекту дома). Отметка чистого пола мокрых помещений — −0,015. Размеры — в миллиметрах, отметки — в метрах, площади — в м²; высоты установки Н от чистого пола своего помещения до оси изделия.
6. Несущие конструкции, общедомовые стояки, вентиляционные каналы и инженерные сети дома настоящим комплектом не изменяются. Работы, затрагивающие их (проём или штраба в несущей стене, перенос стояка, врезка в вентканал, расширение мокрой зоны), выполняются только по отдельному проекту, к которому прилагается техническое заключение о допустимости и безопасности работ, выданное автором проекта дома или организацией с допуском на обследование, и который согласован в установленном порядке (Жилищный кодекс РФ, ст. 25–29).
7. Трассы инженерных сетей на листах — принципиальные. Расчёты электрических нагрузок и токов КЗ, гидравлики, воздухообмена, освещённости и нагрузок на перекрытие выполняются в проектах ЭОМ, ВК, ОВ и КР организацией с допуском СРО; фактические трассы до закрытия отделкой фиксируются исполнительными схемами.
8. Стиль интерьера — Современный (контемпорари). Палитра проекта: основной 60 % — Tikkurila F497 «Paper», Tikkurila J484 «Castle»; дополнительный 30 % — Tikkurila V486 «Claystone»; акцент 10 % — Tikkurila L481 «Silhouette». Коды цвета — по веерам производителей; цвет утверждается по выкрасу на объекте при освещении проекта.
9. Площади поверхностей — по чистым граням стен до отделки: стены = периметр × высоту от чистого пола помещения до низа потолка минус проёмы (облицовка плиткой — до верха облицовки); плинтус = периметр минус дверные проёмы; пол и потолок — по площади помещения. Количество плиток — по раскладке. Способ один для всех листов комплекта (ведомость отделки, колерная карта, раскладка плитки, развёртки).
10. Марки: стены помещения на всех листах — А (верхняя по плану), Б (правая), В (нижняя), Г (левая); марка отделки О — одна на весь альбом; реестр марок отделки (с позициями колерной карты той же отделки) и марки позиций по видам — на листе 89.
11. Развёртки стен выполнены по всем помещениям для стен с электроточками, мебелью, декором и отделкой: санузлы и кухонный фронт — в М 1:25, остальные стены — в М 1:40; расположение развёрток и узлов — на листе 90, узлы — на листе 117.
12. Перечень скрытых работ, на которые составляются акты освидетельствования (форма по приказу Минстроя России № 344/пр): гидроизоляция пола и стен мокрых помещений (с тестом проливом); стяжка пола (толщина, прочность, влажность основания); звукоизоляционные слои и демпферная лента; тёплый пол до заливки (сопротивление, схема укладки); скрытая электропроводка (за потолком и в штробах стен; условия штробления — в следующем пункте); трубопроводы водоснабжения и канализации до закрытия (опрессовка, уклоны); закладные и усиления под подвесные приборы, мебель и тяжёлый декор, рамы инсталляций; каркасы ГКЛ потолков, коробов и перегородок до обшивки.
13. Скрытая электропроводка: за потолком и в штробах стен. Штробы в стенах выполняются только после технического заключения о несущих конструкциях; до заключения несущие стены не определены, и все стены считаются несущими; объём штроб — в ведомости объёмов работ, строка «Штробы в стенах» (вертикальные спуски; объём не меньше фактического, горизонтальные трассы — по исполнительной схеме).
14. Критерии приёмки: допуски отделочных покрытий — по СП 71.13330.2017; испытания систем водоснабжения и канализации — по СП 73.13330.2016 до закрытия трасс; приёмо-сдаточные испытания электроустановки — по ПУЭ, гл. 1.8, с протоколом электролаборатории.
15. Осознанные отступления от ГОСТ Р 21.101-2026, принятые в комплекте: номер листа и число листов («Листов») указаны на каждом листе; на масштабных листах в основной надписи указан фактический масштаб и дан контрольный отрезок 1000 мм; развёртки стен выполнены в М 1:25 и 1:40 (ГОСТ 21.507-81 — 1:50…1:500) ради читаемости привязок; размерные числа и марки элементов (Д-1, ОК-1, О6) — кеглем 2,5 мм, номера помещений — в кружке Ø 8 мм (канон — 3,5 мм и Ø 12 мм): так насыщенные листы А3 читаются без наложений надписей.
16. Графы «Пров.», «Н. контр.», «Утв.» основной надписи заполняются при согласовании комплекта с заказчиком; до согласования комплект подписывает автор проекта (графа «Разраб.»).

Изм.	Кол.уч	Лист	№ док.	Подп.	Дата	ГД-2026-004-АИ		
						Четырёхкомнатная квартира		
						Общая площадь 102,67* м² · * размеры со скана, не замерены (реестр — л. 6–11, ИЗ-8, К-20, К-21)		
Разраб.		Кырлан А.С.			21.10.26	Дизайн-проект интерьера четырёхкомнатной квартиры	Стадия: РП	Лист: 5 / Листов: 124
Пров.								
ГИП		Кырлан А.С.			21.10.26			
Н. контр.						Общие данные — М б/м	Кырлан Александр Сергеевич	
Утв.								

выпуск 05.10.2026 № 7e7a2cd217 · стр. 7 из 168

Открытые вопросы, принятые допущения и конфликты. Лист 1 из 6

Сводка по реестрам координации (стартовое совещание 04.10.2026)

Комплект предварительный по пунктам этих таблиц. Пока по пункту нет ответа или решения, показанное на указанном листе — допущение проектировщика, а не утверждённое решение.
Сводка: открытых вопросов — 23 (из них ждут факта объекта — 14: контрольного обмера, обследования или документа); конфликтов между разделами — 1; изменений в реестре — 19, из них без подписи — 6; разделов, не сданных к выпуску, — 1.
Пункты, ответ на которые лежит на объекте, а не за столом проектировщика (графа «Вид», строка «Ждёт»), собраны на листе «Задание на контрольный обмер и обследование» (листы 12–16): что и где замерить, с какой точностью и чем подтвердить. Пункты, ждущие решения человека, на объекте не закрываются.

Открытые вопросы и принятые допущения

№	Формулировка	Вид	Кто решает	Если решения нет	Лист, где это проявляется
К-1	Окно детской 2 (поз. 9) на наружной стене В: привязки 1580…3080 в источниках нет — в экспликации скана окна этой комнаты не показано. Это допущение проектировщика, центровка, а не замер: окно 1500 мм поставлено примерно по центру наружного участка стены В (по контуру 8030–10610 по оси Х, центр 9320; окно 8540–10040, центр 9290). Размер 1500×1600 и подоконник 800 мм взяты из исходной записи окна, источник размера в данных не указан. Из допущения следует конфликт со стояками Ст К1-2 и Ст В1-2 (9400; 6300) и (9560; 6300): они попадают в проём окна вместе с коробом и люком (конфликт Кф-1, вопрос К-15). Нужен контрольный обмер эркера: положение, размер и подоконник окна, затем осей стояков.	Непонятно Ждёт: обмера	Архитектор-планировщик	Остаётся принятое положение окна как допущение, не замер. Конфликт со стояками Кф-1 не снят: радиатор под окном, шторы и короб со стояками на этом месте не совмещаются.	л. 20 — Обмерный план
К-3	Несущие стены не определены (нет плана БТИ и техзаключения): до их получения демонтаж не планируется. Нужно: запросить проект дома и поэтажный план БТИ, установить серию дома; несущие стены и допустимость вмешательства определяет техническое заключение специализированной организации. Тип дома (монолит) и перекрытие (монолитная плита 220 мм) в данных приняты допущением: источника — проекта дома, плана БТИ, обследования — в материалах объекта нет; материал основания стен и перекрытия определит тот же документ или обследование.	Отсутствует Ждёт: документа, обследования	Архитектор-планировщик	Исходных данных нет: на листе нет решения по этому пункту или оно условное; лист предварительный.	л. 21 — План демонтажа и монтажа перегородок
К-4	Гостиная (поз. 11): мебели в модели нет, расстановка ждёт решения заказчика. Отделка, потолок, свет, розетки и декор выполнены; акцентная стена А L481 возвращена (см. К-7); картина ДК20, ваза ДК21 и подсветка картины — предложение конвейера (ИЗ-7). Площадь по модели 14,55 м² (≈17 м² по реконструкции контура — снимет контрольный обмер).	Отсутствует Ждёт: решения	Дизайнер интерьера	Исходных данных нет: на листе нет решения по этому пункту или оно условное; лист предварительный.	л. 24 — План расстановки мебели
К-5	Гардеробная 1 (поз. 12) в натуре трапеция 2320/2132/1400, в модели прямоугольник той же площади: нужен контрольный обмер углов.	Непонятно Ждёт: обмера	Архитектор-планировщик	Остаётся значение, принятое по исходным данным; оно не подтверждено, лист предварительный.	л. 20 — Обмерный план
К-6	Розетка Р7 (стиральная машина, ванная комната) стоит в 72 мм от угла при норме от 150 мм. Р7 возвращена на прежнее место: стена В, смещение 2543 мм, высота 949 мм — норма ПУЭ 6.6.30 (не выше 1 м) выполнена, флага решения нет; конвейер уходил от угла переносом на 2242 мм и высоту 1250 мм, что нарушало ПУЭ 6.6.30, — этот перенос отменён. Нужно решение автора: сдвинуть машину и розетку от угла или принять 72 мм. Норма для розеток ванной (ПУЭ 7.1.48 против BS 7671) решена: ИЗ-19.	Спорно Ждёт: решения	Инженер-электрик	Р7 остаётся на 2543 мм вдоль стены и 949 мм по высоте, в 72 мм от угла: замечание открыто.	л. 29 — План розеток и электровыводов
К-7	Акцент L481 занимает больше порога 15 % площади поверхностей на акцентной стене А Гостиной — 16 % (проверка по доле акцента, замечание открыто намеренно). Красить плоскость целиком (нужна поддержка в модели), перенести акцент на предметы (в Гостиной они уже есть — ДК20, ДК21, ИЗ-7) или принять 16 %. Для Зала решение принято: 18 % приняты автором (ИЗ-15).	Спорно Ждёт: решения	Колорист-комплектатор	Остаётся акцентная стена L481 в Гостиной, доля 16 % выше порога 15 %; замечание открыто.	л. 58, 59 — Колерная карта
К-8	Графы «Пров.» и «Н. контр.» в штампе пусты: их заполняет человек, подписи проверяющего и нормоконтролёра автор проекта не ставит; для выдачи нужны разные подписанты, отличные от разработчика. Решение автора (ИЗ-18): графы остаются пустыми, комплект предварительный.	Отсутствует Ждёт: решения	Нормоконтролёр	графы остаются пустыми; комплект предварительный, не проверен независимо	л. 2 — Общие данные
К-10	Прямые углы помещений с кухней, санузлами, гардеробными и встроенной мебелью по скану не подтверждены (скос стен приведён к ступеням): ванная комната, тёмная комната, детская 1, коридор, кухня, прихожая-коридор, гардеробная 2, детская 2, гардеробная 1, балкон 1. Нужен контрольный обмер: длины сторон, обе диагонали, отклонения углов от 90° у стен под встроенную мебель и плитку; только после него отмечаются углы 90°.	Отсутствует Ждёт: обмера	Архитектор-планировщик	Исходных данных нет: на листе нет решения по этому пункту или оно условное; лист предварительный.	л. 20 — Обмерный план
К-12	Состав подрядчиков и поставщиков (кто покупает и кто монтирует радиаторы, подоконники, двери, розетки) от заказчика не получен. Принята типовая схема частного ремонта (ИЗ-17): материалы и оборудование покупает заказчик по спецификациям проекта, монтаж ведёт подрядная бригада, приёмку скрытых работ ведёт автор. Схема уточняется договором подряда: нужен договор или состав подрядчиков и поставщиков от заказчика.	Отсутствует Ждёт: решения	Прораб-координатор	остаётся типовая схема: покупает заказчик, монтирует подрядная бригада, скрытые работы принимает автор; закрепление за конкретными подрядчиками не подтверждено	л. 2 — Общие данные
К-13	Детская 2: рабочий стол М36 у стены Б получает боковой свет от окна справа от сидящего; для правши лучше свет слева подтвердить, кто сидит за столом (правша или левша), иначе решить зеркальной расстановкой (нужен перенос двери) либо второй лампой слева.	Спорно Ждёт: решения	Дизайнер интерьера	Остаётся вариант, показанный на листе; он не утверждён, лист предварительный.	л. 24 — План расстановки мебели

						ГД-2026-004-АИ	
						Четырёхкомнатная квартира	
						Общая площадь 102,67* м² · * размеры со скана, не замерены (реестр — л. 6–11, ИЗ-8, К-20, К-21)	
Изм.	Кол.уч	Лист	№ док.	Подп.	Дата	Дизайн-проект интерьера четырёхкомнатной квартиры	Стадия: РП; Лист: 6; Листов: 124
Разраб.		Кырлан А.С.			21.10.26		
Пров.							
ГИП		Кырлан А.С.			21.10.26		
Н. контр.						**Открытые вопросы, принятые допущения и конфликты. Лист 1 из 6** М б/м	**Кырлан Александр Сергеевич**
Утв.							

Открытые вопросы, принятые допущения и конфликты. Лист 2 из 6

Сводка по реестрам координации (стартовое совещание 04.10.2026)

Открытые вопросы и принятые допущения (продолжение)

№	Формулировка	Вид	Кто решает	Если решения нет	Лист, где это проявляется
К-14	Из чего стены под навесными шкафами — Ванная комната (стена Б, М8), Кухня (стена А, М24–М26), Гардеробная 2 (стена В, М33)? Проекта дома нет, на скане материал и толщина не читаются. Нужно обследование: материал основания определяет крепёж (анкер по бетону, закладная в ГКЛ). До ответа материал в данных не указан, замечание открыто намеренно.	Отсутствует Ждёт: вскрытия	Мебельщик	Исходных данных нет: на листе нет решения по этому пункту или оно условное; лист предварительный.	л. 82 — Кухня (пом. 6). Монтажная схема л. 84 — Кухня (пом. 6). Монтажная схема л. 85–87 — Шкафы. Монтажная схема
К-15	Стояки Ст К1-2 и Ст В1-2 (в данных (9400; 6300) и (9560; 6300), короб и люк) попадают в проём окна Детской 2 по стене В (8540–10040): совместить с радиатором под окном и шторами нельзя. Привязку осей стояков от двух стен никто не замерял; в Санузле они не стоят, выпуск унитаза П8 от этого положения — 2,4 м. Нужен контрольный обмер стояков и окна, затем решение: сдвинуть окно, перенести радиатор или обойти короб.	Спорно Ждёт: обмера, затем решения	Инженер ВК (вода, канализация)	Остаются принятые положения окна и стояков без замера; радиатор под окном, шторы и короб со стояками на этом месте не совмещаются.	л. 40 — План выводов сантехники л. 41 — Схема разводки водопровода и канализации л. 20 — Обмерный план
К-17	Ведущий цвет — Paper F497 на стенах и потолке — занимает больше 80 % площади поверхностей в Тёмной комнате (87 %), Гардеробной 2 (89 %), Гардеробной 1 (86 %) и Балконе 1 (85 %): второй цвет почти не читается. Это цвета автора проекта. Принять как есть или задать этим помещениям второй цвет.	Спорно Ждёт: решения	Колорист-комплектатор	Остаются цвета автора: стены и потолок в Paper F497, доля ведущего цвета 85–89 %.	л. 58, 59 — Колерная карта
К-18	Вытяжка М25 встроена в навесной модуль на отметке 1550 мм: её низ над электрической варочной панелью 610 мм, а фартук 650 мм при практике 450–600 мм. Модель вытяжки не выбрана, паспорта нет, допустимая высота над варочной неизвестна. Поднять модуль М25 (и соседние М24, М26 — на единую отметку), либо выбрать вытяжку, допускающую 610 мм по паспорту.	Спорно Ждёт: данных закупки, затем решения	Мебельщик	Остаётся модуль на отметке 1550 мм; низ вытяжки 610 мм над панелью, меньше 650 мм; допустимость высоты не подтверждена.	л. 81 — Кухня (пом. 6). Развёртка гарнитура
К-19	Привязка угла помещения «Гостиная» (поз. 12 скана; в примечании проекта названо «зал») принята в точке (10670; 3470) мм — это допущение, не замер: по пиксельной привязке скана угол может лежать примерно на 700 мм левее. От этой точки по оси X отсчитываются Гостиная и Гардеробная 1, по ней же проходит стена Детской 2 со стороны Гостиной. Нужен контрольный обмер: расстояние от опорной стены до этого угла.	Непонятно Ждёт: обмера	Архитектор-планировщик	Остаётся угол в точке (10670; 3470) как допущение: размеры правой части на листах — расчётные, возможен сдвиг до ≈700 мм; мебель, свет и розетки там привязаны к принятым координатам.	л. 20 — Обмерный план
К-20	Наружные скошенные стены (в натуре под 45°) заменены на планах ступенями: движок описывает только ортогональную геометрию. Гостиная — три ступени, площадь по модели 14,55 м² против ≈17 м² по реконструкции контура; Гардеробная 1 — прямоугольник 1400×2230 вместо трапеции 2320/2132/1400 той же площади (К-5). Углы и длины скосов на листах не показаны, площади у скошенных стен условные (К-10). Принять ступени как условность до обмера или передать скосы обмером и отдельным чертежом.	Спорно Ждёт: решения	Архитектор-планировщик	Остаются ступени вместо скоса: фактическая форма наружных стен Гостиной и Гардеробной 1 на листах не показана, размеры вдоль скоса брать по обмеру на месте.	л. 20 — Обмерный план л. 24 — План расстановки мебели
К-21	Все размеры сняты с размерных цепочек растрового скана заказчика, контрольного обмера нет. Площади помещений и «Общая площадь 102,67 м²» в штампе каждого листа — расчётные по модели, не обмерные: итог зависит от ступеней вместо скоса (К-20) и принятого угла Гостиной (К-19). Названия и номера помещений со сканом не сверены (общая комната назначена решением автора, ИЗ-13). Толщины стен приняты допущением: наружные 250 мм, внутренние 120 мм, источника (обмер, проект дома) нет. Всё, что на листах выглядит как замер, снято со скана.	Отсутствует Ждёт: обмера	Архитектор-планировщик	Размеры и площади остаются ориентировочными; штамп печатает «Общая площадь 102,67 м²» как расчётную величину, не подтверждённую обмером; до обмера не заказывать материалы и изделия по размерам листов.	л. 2 — Общие данные л. 20 — Обмерный план
К-22	Окно Гостиной (пом. 11) на стене В, часть 2: остекление показано по обмерному скану, размеры 1500×1600 мм и подоконник 900 мм приняты типовыми, не замерены. Нужен контрольный обмер окна: положение, ширина, высота, подоконник.	Непонятно Ждёт: обмера	Архитектор-планировщик	Остаются типовые размеры окна 1500×1600 мм, подоконник 900 мм; на плане они напечатаны как принятые, не замеренные.	л. 20 — Обмерный план
К-23	Две розетки выше 1 м от пола остаются предложением проектировщика, решения автора нет: Р21 (вытяжка М25, 2200 мм, в модуле за съёмной панелью, Кухня) и Р27 (слаботочный щит ЩС, 1600 мм, Прихожая-коридор). Основание — назначение розетки; автор высоту не подтверждал; основание записано в самой позиции (знак «**» у марки, примечание листа). Норма (ПУЭ, п. 6.6.30) — не выше 1 м. Подтвердить высоты или опустить розетки.	Спорно Ждёт: решения	Инженер-электрик	Высоты остаются как на листе, решение автором не подтверждено.	л. 29 — План розеток и электровыводов л. 32, 33 — Ведомость электроточек и изделий
К-24	Высота потолка 2700 мм принята: источника (замер, проект дома) в материалах объекта нет. От неё зависят вертикальные размеры альбома: развёртки, шкафы и встроенная мебель, плитка, потолки, объёмы работ. Замерить высоту на объекте в каждом помещении.	Непонятно Ждёт: обмера	Архитектор-планировщик	Высота 2700 мм остаётся принятой, не замеренной: вертикальные размеры листов и объёмы работ ориентировочные; встроенную мебель и плитку по высоте не заказывать до замера.	л. 20 — Обмерный план
К-25	Разрешённая мощность 15 кВт принята, технических условий в материалах объекта нет; расчётная мощность 11,2 кВт. Сверить с техническими условиями.	Непонятно Ждёт: документа	Инженер-электрик	Разрешённая мощность 15 кВт остаётся принятой, не подтверждённой техническими условиями: вводной аппарат и группы щита предварительные.	л. 34, 35 — Однолинейная схема щита

Изм.	Кол.уч	Лист	№ док.	Подп.	Дата
Разраб.		Кырлан А.С.			21.10.26
Пров.					
ГИП		Кырлан А.С.			21.10.26
Н. контр.					
Утв.					

ГД-2026-004-АИ

Четырёхкомнатная квартира

Общая площадь 102,67* м² · * размеры со скана, не замерены (реестр — л. 6–11, ИЗ-8, К-20, К-21)

Дизайн-проект интерьера четырёхкомнатной квартиры

Стадия	Лист	Листов
РП	7	124

Открытые вопросы, принятые допущения и конфликты. Лист 2 из 6

М б/м

Кырлан Александр Сергеевич

выпуск 05.10.2026 № 7e7a2cd217 · стр. 9 из 168

Открытые вопросы, принятые допущения и конфликты. Лист 3 из 6

Сводка по реестрам координации (стартовое совещание 04.10.2026)

Открытые вопросы и принятые допущения (продолжение)

№	Формулировка	Вид	Кто решает	Если решения нет	Лист, где это проявляется
К-26	Артикулы изделий отделки не выбраны. Инженерная доска (пом. 1, 3, 4, 6, 8, 9, 11, 12), керамогранит пола (пом. 2, 5, 7, 10, 13), керамогранит стен санузла и ванной (пом. 2, 10) и фартука кухни (пом. 6), плинтус МДФ (пом. 1, 3–9, 11, 12), плинтус из керамогранита (пом. 13) и краска акцентных стен (пом. 1, 11) заданы характеристиками — «аналог по характеристикам», кода изделия производителя нет. Цвет керамогранита назван тоном по колерной карте (J484, F497, V486), но тон — не артикул изделия. Артикул выбирается при закупке: выбрать изделия, вписать артикулы в ведомость отделки и спецификации, цвет и тон принять по образцу из партии. Количество к заказу и упаковки — расчётные, по номинальным размерам, до выбора изделия.	Отсутствует Ждёт: данных закупки, затем решения	Отделочник	материалы остаются описанными характеристиками; заказ по спецификации и подсчёт упаковок — только после выбора изделий	л. 49 — Раскладка плитки. Планы полов л. 50 — Раскладка плитки. Фартук кухни л. 51 — Раскладка плитки. Ванная комната. Развёртки стен л. 52 — Раскладка плитки. Санузел. Развёртки стен л. 53 — План полов л. 55–57 — Ведомость отделки помещений л. 58, 59 — Колерная карта л. 60, 61 — Спецификация отделочных материалов л. 89 — Реестр марок отделки и позиций альбома л. 121, 122 — Спецификация материалов л. 123, 124 — Смета ориентировочная
К-27	Модели встраиваемой техники кухни не выбраны: холодильник (М20), духовой шкаф (М22) и посудомоечная машина (М27) заданы описанием «аналог по характеристикам» — без производителя, серии и кода. Размеры ниш и вентзазоры взяты по типовой схеме на 600 мм, а не по паспорту модели: у разных изготовителей они расходятся, и модуль, сделанный по типовой нише, может не принять выбранную технику. Вытяжка М25 — отдельный вопрос К-18. Нужно: выбрать модели, получить монтажные схемы изготовителей и сверить ниши модулей, вентиляцию и подключение до заказа гарнитура.	Отсутствует Ждёт: данных закупки, затем решения	Мебельщик	ниши остаются по типовой схеме на 600 мм, не подтверждённой паспортом модели; модули кухни не заказывать до выбора техники	л. 81 — Кухня (пом. 6). Развёртка гарнитура л. 82 — Кухня (пом. 6). Монтажная схема

Конфликты между разделами

№	Формулировка	Разделы	Статус	Кто решает	Если решения нет	Лист, где это проявляется
Кф-1	Стояки Ст К1-2, Ст В1-2 с коробом и люком попадают в проём окна Детской 2 (стена В, 8540–10040): положение стояков и окна не замерено; вопрос К-15.	ВК; архитектура (окно Детской 2)	Открыт, круг 1	Инженер ВК (вода, канализация)	Положение окна — допущение, стояков — по скану без привязки; пока их не замерили, окно, радиатор под ним и короб со стояками на листах не согласованы.	л. 40 — План выводов сантехники л. 41 — Схема разводки водопровода и канализации

Изм.	Кол.уч	Лист	№ док.	Подп.	Дата
Разраб.		Кырлан А.С.			21.10.26
Пров.					
ГИП		Кырлан А.С.			21.10.26
Н. контр.					
Утв.					

ГД-2026-004-АИ

Четырёхкомнатная квартира

Общая площадь 102,67* м² · * размеры со скана, не замерены (реестр — л. 6–11, ИЗ-8, К-20, К-21)

Дизайн-проект интерьера четырёхкомнатной квартиры

Стадия	Лист	Листов
РП	8	124

Открытые вопросы, принятые допущения и конфликты. Лист 3 из 6

М б/м

Кырлан Александр Сергеевич

выпуск 05.10.2026 № 7e7a2cd217 · стр. 10 из 168

Открытые вопросы, принятые допущения и конфликты. Лист 4 из 6

Сводка по реестрам координации (стартовое совещание 04.10.2026)

Изменения проекта после выпуска листов (реестр изменений)

№	Дата	Лист	Было	Стало	Кто решил, подпись
ИЗ-1	05.10.2026	л. 24 — План расстановки мебели	Окно Детской 2 на стене Б (смещение 900). Стол М36 1400×650, стена Б, смещение 1000; кресло М37 (9300; 4950); стеллаж М38 1200×2100, стена В, смещение 960.	Окно на наружной стене В (1580…3080; положение — допущение, центровка, не замер). Стол М36 1400×650 (размер и допуск глубины «Г 600–700» прежние), стена Б, смещение 1500; кресло М37 (9150; 5450); стеллаж М38 1200×2100 (размер прежний), стена Б, смещение 120. Основания. Стеллаж: на стене В теперь окно, прежнее место перекрывает проём; на стене Б он стоит в углу А/Б. Стол: перенесён вслед за окном на стену Б без изменения размера; при 650 мм край стола заходит на 20 мм в проекцию проёма окна — это не нарушение, принято автором 05.10.2026 (вопрос К-16 закрыт). Вместе с окном изменились: направление паркета в Детской 2 (по оси X → по оси Y, вдоль света от окна), портьеры и римская штора Т16, Т17 (длина, карниз). Декор: спатифиллум ДК16 перенесён с (9900; 6100) на (10200; 4300), основание в данных не записано. Окно, стол М36, кресло М37, стеллаж М38, портьеры Т16, Т17, декор ДК16 и направление паркета помечены знаком предложения.	Утверждено: Кырлан А.С., автор проекта, 05.10.2026 — утверждены положение и размеры мебели «Детской 2»: стол М36 1400 × 650 (заход края стола на 20 мм в проекцию проёма окна принят), кресло М37, стеллаж М38 1200 × 2100. Не утверждены (допущение или предложение): положение окна, портьеры Т16 и Т17, декор ДК16, направление паркета. решение автора проекта, оформлено исполнителем по его поручению (запись внесена конвейером, на утверждение А. С. Кырлана)
ИЗ-2	05.10.2026	л. 29 — План розеток и электровыводов л. 30 — План освещения л. 31 — План выключателей и схема включения л. 43 — Спецификация светильников и сценарии освещения	Детская 2: общий свет L15 (шесть спотов), выключатель S14 (L15 и свет санузла). Бра и отдельных линий у кровати и у стола не было.	Добавлены: бра Св63 у изголовья кровати М34 (стена А, смещение 510, высота 1400 мм, 6 Вт, 2700 К, линия L21) и выключатель S17 (стена А, смещение 1050, высота 900 мм); бра Св67 над рабочим столом М36 (стена Б, смещение 2200, высота 1300 мм, 7 Вт, 3000 К, линия L22) и выключатель S18 (стена Б, смещение 1410, высота 900 мм). S18 стоял на смещении 1350 мм и оказывался за стеллажом М38 1200×2100: стеллаж возвращён к прежнему размеру, выключатель перенесён в просвет между стеллажом и столом. Заказчик бра не заказывал, основание в данных не записано; позиции помечены как предложение проектировщика.	Утверждено: Кырлан А.С., автор проекта, 05.10.2026 — утверждён перенос выключателя S18 в просвет между стеллажом М38 и столом М36 (стеллаж прежнего размера 1200 × 2100). Не утверждены (предложение проектировщика): бра Св63 и Св67, выключатели S17 и S18 как позиции, линии L21 и L22. решение автора проекта, оформлено исполнителем по его поручению (запись внесена конвейером, на утверждение А. С. Кырлана)
ИЗ-3	05.10.2026	л. 30 — План освещения л. 43 — Спецификация светильников и сценарии освещения	Санузел: общий свет L12 (спот Св51), света у зеркала не было.	Добавлен светильник Св64 над зеркалом ДК17 (стена Б, смещение 600, высота 1950 мм, 8 Вт, 3000 К, IP44, драйвер встроен, линия L12, группа 4). Основание: (свет у зеркала в санузле). Заказчик светильник не заказывал; решение исполнителя, знак «**» у Св64 остаётся.	Утверждено: исполнитель по поручению Кырлана А.С., 05.10.2026. решение исполнителя
ИЗ-4	05.10.2026	л. 31 — План выключателей и схема включения л. 43 — Спецификация светильников и сценарии освещения	Зал: выключатель S2 (лента в карнизе L3) без светорегулятора, сценариев света нет.	В S2 добавлен светорегулятор (тип ТЕ, под диммируемую ленту); записаны четыре сценария света: «Вечер» (L1 0 %, L2 100 %, L3 50 %), «Гости» (100/100/100 %), «Кино» (0/0/20 %), «Уборка» (100/100/0 %). Основание: (гостиная с тремя и более группами света — сценарий; в Зале L1–L3) и (промежуточный уровень — группе на светорегуляторе). Уровни выбрал исполнитель, заказчик их не задавал; знак «**» у S2 остаётся. Сценарии и диммер записаны для Зала; в Гостиной их нет.	Утверждено: исполнитель по поручению Кырлана А.С., 05.10.2026. решение исполнителя
ИЗ-5	05.10.2026	л. 34, 35 — Однолинейная схема щита л. 29 — План розеток и электровыводов л. 32, 33 — Ведомость электроточек и изделий	Розетки Гостиной Р36–Р38 — в группе 9 «розетки фартука кухни». Щит ЩРВ-П-54 на 54 модуля, занято 42.	Новая группа 19 «розетки гостиной»: автомат С16, УЗО 30 мА типа А, кабель ВВГнг(А)-LS 3×2,5, 1,0 кВт, длина линии 30 м (оценка, не замер). Щит ЩРВ-П-72 на 72 модуля, занято 44. Основание щита: при 44 занятых модулях резерв ЩРВ-П-54 составил бы 10 модулей (18,5 %) — меньше 20 %. Основание группы 19: (не больше 12 гнёзд на группу 2,5 мм²; практика): с Р36–Р38 в группе 9 было бы 14 гнёзд, осталось 8. Знак «**» у щита и Р36–Р38 остаётся.	Не утверждено: подписи нет. решение исполнителя
ИЗ-6	05.10.2026	л. 22 — План дверей и ведомость заполнения проёмов л. 24 — План расстановки мебели	Гардеробная 1: дверь в Гостиную, проём 1420 мм по скану, полотно распашное 1420 мм.	Полотно раздвижное, две створки по 710 мм по накладной направляющей; проём 1420 мм прежний. Основание: распашное полотно 1420 мм в помещении 1400×2230 задевало стеллаж М39. Заказчик замену не заказывал; решение исполнителя, знак предложения у двери остаётся.	Утверждено: исполнитель по поручению Кырлана А.С., 05.10.2026. решение исполнителя
ИЗ-7	05.10.2026	л. 23 — Концепция интерьера л. 58, 59 — Колерная карта л. 30 — План освещения л. 31 — План выключателей и схема включения	Гостиная: акцентная стена А в L481 (finish.accent); предметов декора и подсветки картины не было; выключатель S16 одноклавишный (L19).	Конвейер заменял акцентную стену предметами и ради порога снял её; решением от 05.10.2026 акцентная стена А возвращена (доля 16 % выше порога 15 %, замечание открыто, К-7). Предметы оставлены как предложение: картина ДК20 (стена Г, 800×600), ваза ДК21, подсветка картины Св65, Св66 (линия L20), вторая клавиша S16, подсветка помечена как предложение проектировщика. Нужны ли предметы при акцентной стене — решает автор.	Не утверждено: подписи нет. ИИ-конвейер, на утверждение А. С. Кырлана

Изм.	Кол.уч	Лист	№ док.	Подп.	Дата
Разраб.		Кырлан А.С.			21.10.26
Пров.					
ГИП		Кырлан А.С.			21.10.26
Н. контр.					
Утв.					

ГД-2026-004-АИ

Четырёхкомнатная квартира

Общая площадь 102,67* м² · * размеры со скана, не замерены (реестр — л. 6–11, ИЗ-8, К-20, К-21)

Дизайн-проект интерьера четырёхкомнатной квартиры

Стадия	Лист	Листов
РП	9	124

Открытые вопросы, принятые допущения и конфликты. Лист 4 из 6

М б/м

Кырлан Александр Сергеевич

Открытые вопросы, принятые допущения и конфликты. Лист 5 из 6

Сводка по реестрам координации (стартовое совещание 04.10.2026)

Изменения проекта после выпуска листов (реестр изменений) (продолжение)

№	Дата	Лист	Было	Стало	Кто решил, подпись
ИЗ-8	05.10.2026	л. 20 — Обмерный план л. 29 — План розеток и электровыводов л. 30 — План освещения	Наружный контур: ступени по осям 14780, 7710, 6540, 7970 мм. Прихожая-коридор: розетка Р27 на стене Г, смещение 1990; ИП5 (5600; 3800). Коридор: ИП3 (8500; 3200), выключатель S4 смещение 870. Детская 1: Св20, Св25 по X 14450. Ванная: Св13 по X 7700, дверь смещение 100. Детская 2: Р33 смещение 3140 мм.	Ступени контура 14840, 7770, 6600, 8030 мм (+60 мм): приведены к крайним граням помещений модели (Детская 1, Санузел); после этого окна Гостиной, Детской 1 и Детской 2 лежат на гранях контура. Р27 на стене А, смещение 1750; ИП5 (5500; 4400), ИП3 (8300; 2850). Св20, Св25 по X 14400 и Св13 по X 7600. Дверь ванной смещение 110. Р33 на смещении 1100 мм: прежнее место попало в проём перенесённого окна (ИЗ-1). S4 смещение 880: вслед за дверью ванной (110 вместо 100), зазор от откоса до выключателя прежний, 70 мм. Сдвиги — решение исполнителя; знак «**» у сдвинутых позиций остаётся.	Не утверждено: подписи нет. решение исполнителя
ИЗ-9	05.10.2026	л. 29 — План розеток и электровыводов л. 30 — План освещения л. 20 — Обмерный план	Слаботочные точки (5 шт.) без слаботочного щита; точек доступа Wi-Fi не было; параметров щита ЩС в данные проекта не было.	Добавлены: слаботочный щит ЩС (Прихожая-коридор, стена А, смещение 1380, высота 1600 мм), точки доступа АР1 (5500; 5000) и АР2 (13000; 4300), кабель U/UTP кат. 6 у LAN4 и в данные проекта, щит ЩС: глубина 150 мм, пластик, вентилируемый, роутер внутри. Основание: (нет щита) и (ориентир две точки доступа на 102 м²). Заказчик слаботочку в таком составе не заказывал; решение исполнителя, знак «**» у ЩС, АР1, АР2 и LAN4 остаётся. Две точки Wi-Fi и тип щита автор не выбирал.	Не утверждено: подписи нет. решение исполнителя
ИЗ-10	05.10.2026	л. 29 — План розеток и электровыводов л. 32, 33 — Ведомость электроточек и изделий	Кухня: розетка Р21 (вытяжка М25) на высоте 2200 мм, решение, назначение «вытяжка М25».	Назначение «вытяжка М25 (в модуле, съёмная панель)» и признак доступа access: true. Высота 2200 мм прежняя, знак предложения прежний, флаг «решение» снят: решающего нет; высота автором не подтверждена, вопрос К-23.	Не утверждено: подписи нет. решение исполнителя
ИЗ-11	05.10.2026	л. 24 — План расстановки мебели л. 58, 59 — Колерная карта	Марки декора Д1…Д19 (совпадали с префиксом дверей Д). Образцов колерной карты 10.	Марки декора ДК1…ДК19, позиции не менялись. Добавлен образец № 11 (J484, Tikkurila): отдельный выкрас плинтуса коридора и прихожей на МДФ.	Не утверждено: подписи нет. решение исполнителя
ИЗ-12	24.09.2026	л. 29 — План розеток и электровыводов л. 32, 33 — Ведомость электроточек и изделий	В ванной комнате и санузле не было вывода к вентилятору вытяжки и коробки уравнивания потенциалов.	Добавлены выводы к вентиляторам: ЭВ2 (ВР1, ванная комната) и ЭВ5 (ВР3, санузел) — группа 4, высота 2550 мм, IP44, включение с основным светом, таймер выбега в вентиляторе; коробки уравнивания потенциалов КУП1 (ванная комната) и КУП2 (санузел) — высота 300 мм, у входа, вне зон 0–2. Основание: правила проверки (питание вентилятора вытяжки мокрого помещения) и (КУП в помещении с ванной или душем). Заказчик эти позиции не заказывал; решение исполнителя, ЭВ2, ЭВ5, КУП1 и КУП2 со знаком «**».	Утверждено: исполнитель по поручению Кырлана А.С., 05.10.2026. решение исполнителя
ИЗ-13	05.10.2026	л. 24 — План расстановки мебели л. 20 — Обмерный план	Общая комната квартиры не названа: «Зал» (18,16 м²) или «Гостиная» (14,55 м²); если бы общей считалась «Гостиная», норма 16 м² не выполнялась (вопрос К-9).	Общей комнатой назначен «Зал» (18,16 м²): он больше «Гостиной», проходит норму общей комнаты не менее 16 м² (СП 54.13330.2022, п. 5.11) и по концепции интерьера несёт обеденную группу на шесть персон. «Гостиная» (14,55 м²) остаётся второй жилой комнатой: для неё действует норма спальни 8 м², она выполнена. Названия и номера помещений со сканом по-прежнему не сверены (К-21).	Утверждено: Кырлан А.С., автор проекта, 05.10.2026. решение автора проекта, оформлено исполнителем по его поручению
ИЗ-14	05.10.2026	л. 20 — Обмерный план л. 22 — План дверей и ведомость заполнения проёмов	Санузел (поз. 10) в эркере соединён только с «Детской 2»: другого входа нет; вход в помещение с унитазом из жилой комнаты расходится с требованием СП 54 (вопрос К-2).	Сохраняется существующее положение: вход в санузел — из «Детской 2», перепланировка с тамбуром не выполняется. Основание: требование СП 54.13330.2022 (формулировка не сверена с первоисточником) не допускает устраивать вход в помещение с унитазом из жилой комнаты; проект нового входа не устраивает, а оставляет существующий. Тамбур отнял бы площадь «Детской 2», а стены до технического заключения считаются несущими (К-3). Существующий вход взят с обмерного скана заказчика, на объекте не проверен (К-21). Это отступление от требования, рассчитанного на новое строительство, принято как существующее положение; проверка по этому пункту остаётся замечанием.	Утверждено: Кырлан А.С., автор проекта, 05.10.2026. решение автора проекта, оформлено исполнителем по его поручению
ИЗ-15	05.10.2026	л. 58, 59 — Колерная карта л. 24 — План расстановки мебели	Зал: акцентная стена А (ТВ-стена, L481) занимает 18 % площади поверхностей при пороге акцента 15 % (вопрос К-7).	Доля акцента 18 % принята: ТВ-стена А красится в L481 целиком, это замысел автора, на предметы акцент не переносится. Порог 15 % практики 60/30/10 превышен сознательно. Акцентная стена «Гостиной» (16 %) этим решением не затронута — вопрос К-7.	Утверждено: Кырлан А.С., автор проекта, 05.10.2026. решение автора проекта, оформлено исполнителем по его поручению
ИЗ-16	05.10.2026	л. 2 — Общие данные	Состав выдачи не подтверждён: разделы пожарного инженера, акустика, технадзора, слаботочки и допуск ГИПа в сводке ролей числились не сданными (вопрос К-11).	Пожарный инженер, акустик и технадзор в заказ частного ремонта квартиры не входят: роли отмечены в сводке ролей пропущенными, с причиной. Слаботочка входит в состав: выпущен лист «План слаботочных сетей»; отдельная ведомость слаботочки (кабельный журнал, состав слаботочного щита) ролью не сдана и остаётся в таблице несданных разделов. Функции ГИП выполняет автор проекта, графа «ГИП» основной надписи заполнена его фамилией; членство в СРО не проверялось.	Утверждено: Кырлан А.С., автор проекта, 05.10.2026. решение автора проекта, оформлено исполнителем по его поручению

						ГД-2026-004-АИ	
						Четырёхкомнатная квартира	
						Общая площадь 102,67* м² · * размеры со скана, не замерены (реестр — л. 6–11, ИЗ-8, К-20, К-21)	
Изм.	Кол.уч	Лист	№ док.	Подп.	Дата	Дизайн-проект интерьера четырёхкомнатной квартиры	Стадия: РП; Лист: 10; Листов: 124
Разраб.		Кырлан А.С.			21.10.26		
Пров.							
ГИП		Кырлан А.С.			21.10.26	**Открытые вопросы, принятые допущения и конфликты. Лист 5 из 6** М б/м	**Кырлан Александр Сергеевич**
Н. контр.							
Утв.							

Открытые вопросы, принятые допущения и конфликты. Лист 6 из 6

Сводка по реестрам координации (стартовое совещание 04.10.2026)

Изменения проекта после выпуска листов (реестр изменений) (продолжение)

№	Дата	Лист	Было	Стало	Кто решил, подпись
ИЗ-17	05.10.2026	л. 2 — Общие данные	Матрицы ответственности (делает / поставляет / принимает / хранит) нет; кто покупает и кто монтирует — не определено (вопрос К-12).	Принята типовая схема частного ремонта: материалы и оборудование покупает заказчик по спецификациям проекта; монтаж ведёт подрядная бригада; приёмку скрытых работ ведёт автор проекта. Распределение закреплено по радиаторам, подоконникам, дверям, розеткам и выключателям, сантехническим приборам, светильникам и отделочным материалам. Схема уточняется договором подряда; состав подрядчиков и поставщиков остаётся вопросом К-12.	Утверждено: Кырлан А.С., автор проекта, 05.10.2026. решение автора проекта, оформлено исполнителем по его поручению
ИЗ-18	05.10.2026	л. 2 — Общие данные	Графы «Пров.» и «Н. контр.» основной надписи пусты (вопрос К-8); как с ними поступать — не записано.	Графы «Пров.» и «Н. контр.» остаются пустыми: независимой проверки и нормоконтроля проекта не было, автор проекта сам себе их не подписывает. Комплект выпускается предварительным: пока нет подписи проверяющего и нормоконтролёра, отличных от разработчика, он не считается окончательным.	Утверждено: Кырлан А.С., автор проекта, 05.10.2026. решение автора проекта, оформлено исполнителем по его поручению
ИЗ-19	05.10.2026	л. 29 — План розеток и электровыводов л. 32, 33 — Ведомость электроточек и изделий	Розетки ванной Р7 (стиральная машина) и Р8 (фен): по ПУЭ допустимы в зоне 3 через УЗО 30 мА, по британской норме BS 7671 (п. 701.512.3) — дальше 2,5 м от границы зоны 1; какая норма принята — вопрос К-6.	Принята норма ПУЭ (п. 7.1.48): розетки в зоне 3 помещения с ванной допустимы при защите УЗО 30 мА. Положение розеток не менялось. Основание: розетки вне зон 0–2 (до границы зоны 1: Р7 1630 мм, Р8 — 1441 мм), исполнение IP44, группы 14 и 15 защищены УЗО 30 мА типа А. Это сознательное отступление от зарубежной нормы BS 7671: в России она не действует, по ней в таком месте допустима только бритвенная розетка с разделительным трансформатором. Расстояние Р7 до угла (72 мм при норме от 150 мм) этим решением не затронуто — вопрос К-6.	Утверждено: Кырлан А.С., автор проекта, 05.10.2026. решение автора проекта, оформлено исполнителем по его поручению

Разделы, не сданные к выпуску (сводка ролей)

№	Раздел	Состояние	Причина
1	Инженер слаботочки и умного дома	Не сдан	слаботочка входит в состав заказа (ИЗ-16); выпущен лист «План слаботочных сетей» (раздел электрика); отдельная ведомость слаботочки — кабельный журнал, состав слаботочного щита — не выпущена

Примечания

1. Номера листов — по ведомости рабочих чертежей комплекта (лист «Общие данные»).
2. Графа «Если решения нет» показывает состояние решения на листах; влияние на сроки и стоимость по пунктам не оценивалось.
3. Пункт, по которому принято решение, при следующем выпуске комплекта из таблиц исключается.

Изм.	Кол.уч	Лист	№ док.	Подп.	Дата
Разраб.		Кырлан А.С.			21.10.26
Пров.					
ГИП		Кырлан А.С.			21.10.26
Н. контр.					
Утв.					

ГД-2026-004-АИ

Четырёхкомнатная квартира

Общая площадь 102,67* м² · * размеры со скана, не замерены (реестр — л. 6–11, ИЗ-8, К-20, К-21)

Дизайн-проект интерьера четырёхкомнатной квартиры

Стадия	Лист	Листов
РП	11	124

Открытые вопросы, принятые допущения и конфликты. Лист 6 из 6

М б/м

Кырлан Александр Сергеевич

Задание на контрольный обмер и обследование. Лист 1 из 5

ПРЕДВАРИТЕЛЬНО · не для производства работ · открыто пунктов: 30 (реестр — л. 6–11)

Что замерить, вскрыть и получить до заказа материалов и изделий

Задание собрано из открытых вопросов, ответ на которые лежит на объекте или в документах, а не за столом проектировщика. Пока факт не получен, размер, материал или положение на листах — допущение (знак «*»), а не замер.
Сводка: на объекте — 17 (до демонтажа — 12; после демонтажа — 3; после черновых работ — 2); документом и при закупке — 5; из допущений в данных и на листах — 12, из них без вопроса в реестре — 5. Закрываются вопросы: К-1, К-3–К-5, К-10, К-13–К-15, К-18–К-22, К-24–К-27 (17). Вопросы, ждущие решения человека, задание не закрывает — они решаются по реестру открытых вопросов.

Условия проведения

Порядок работ	Приёмы и точность	Кто присутствует	Если факт не совпал с проектом
1. До демонтажа — существующее состояние: контур, диагонали, высоты, проёмы, оси стояков, ниши и конструкции, которые видны. 2. После демонтажа, до черновых работ — то, что закрывали отделка и короба: основание стен, фактические толщины, углы, узлы. 3. После черновых работ, до чистового пола — габариты кухни и встроенной мебели по готовым стенам: после штукатурки и выравнивания размеры отличаются от размеров до работ. 4. Документы и данные закупки — не на объекте: к сроку из последней таблицы, от них зависят привязки и заказ. Что заказывается по размеру из задания, до закрытия пункта не заказывают: сроки изготовления — по графику закупок прораба.	Обход по часовой стрелке от входа: стены, проёмы, потолок, коммуникации (стояки, щиток, вентканалы), особенности (ниши, короба, выступы). Размеры записывают в мм; сумма участков равна общему размеру, при цепочке длиннее трёх участков ставят проверочный (общий) размер. Диагонали каждого помещения; если две диагонали различаются на 5 мм и больше, разницу подписывают на плане. Потолок — в нескольких точках: центр, углы, у проёмов. Проём — ширина, высота, глубина откоса, привязка к ближайшим углам, высота подоконника. Допустимая погрешность прибора — 2–3 мм на метр; размеры округляют кратно 5 мм; два контрольных промера одного размера не должны расходиться более чем на 2 %. Допуск по пункту — в графе «Точность». План БТИ обмер не заменяет.	Прораб (отвечает за проведение) — назначает день и порядок обхода, открывает объект и освобождает помещения, ведёт это задание и реестр изменений. Архитектор — выполняет обмер, составляет акт контрольного обмера и подписывает результаты по размерам и конструкциям. Владельцы вопросов присутствуют при пунктах своего раздела или принимают результат до заказа: Дизайнер интерьера — К-4, К-13, К-20, К-21; Мебельщик — К-14, К-18, К-27; Инженер ВК (вода, канализация) К-1, К-15; Инженер-электрик — К-25; позиции О-1; Отделочник — К-26; позиции О-13, О-14; Инженер ОВ — позиции О-2, О-3. Технадзор — при вскрытиях и обследованиях: фото с рулеткой до закрытия. Заказчик или его представитель — передаёт документы (план БТИ, проект дома, технические условия, паспорта), подписывает акт. Проектных решений на обмере не принимают: обмер даёт факт, решения — по реестру открытых вопросов (листы 6–11).	1. В пределах допуска пункта — принимается измеренное значение, лист перевыпускается, знак «*» снимается. 2. Больше допуска или контрольные промеры расходятся более чем на 2 % — промер повторяют; не подтвердилось — запись в реестр изменений (дата, лист, было, стало, кто решил, подпись), работы в этом месте не начинают. 3. Затронуты несущая стена, стояк, вентканал или мокрая зона — сразу владельцу раздела и ГИПу (главному инженеру проекта); между разделами не больше двух кругов, затем решает ГИП. 4. На объекте устно ничего не согласуется: каждое решение — записью в реестр с подписью.

Этап 1. До демонтажа

№	Где	Способ	Что сделать	Кто выполняет	Точность	Что пересчитается в альбоме	Чем подтверждается	Закрывает вопросы реестра
О-1	Вход в квартиру или лестничная клетка; место щита на плане	Обмер	Существующий щиток и счётчик электроэнергии: место и габарит ниши, состояние ввода, марка и сечение вводного кабеля, наличие вводного автомата и УЗО, пломбы.	Архитектор	±5 мм	Ниша и место щита на листах; вводной кабель и аппараты на однолинейной схеме; расстояния до первых групп. Листы: л. 34, 35 — Однолинейная схема щита	акт контрольного обмера; фото с рулеткой и привязкой к стене или углу	Вопроса в реестре нет: Альбом принимает щит и ввод без осмотра. Результат принимает: Инженер-электрик
О-2	Зал (пом. 1), Детская 1 (пом. 4), Кухня (пом. 6), Детская 2 (пом. 9), Гостиная (пом. 11); у окон	Обмер	Положение стояков отопления (подающий и обратный) от граней стен, диаметры, наличие запорной арматуры; существующие радиаторы: число секций, межосевое расстояние, подводки. В данных стояков отопления нет — лист отопления выводит их условно у откоса окна, радиаторы — «принципиально, по расчёту».	Архитектор	±5 мм	План отопления: места стояков и подводок, привязки радиаторов; подбор радиаторов по теплотехническому расчёту; радиаторы и узлы подключения в ВОР и спецификации. Листы: л. 39 — План отопления	акт контрольного обмера; фото с рулеткой и привязкой к стене или углу	Вопроса в реестре нет: Альбом принимает положение стояков и радиаторов отопления без обмера. Результат принимает: Инженер ОВ
О-3	Ванная комната (пом. 2), Кухня (пом. 6), Санузел (пом. 10)	Обмер	Положение и сечение вентканалов кухни и санузлов, проверка тяги (по листку бумаги или анемометром), состояние решёток. В данных каналов нет: лист вентиляции ставит решётки и вход вытяжки у стояков по практике.	Архитектор	±5 мм	План вентиляции: места решёток и вход вытяжки; воздухообмен по помещениям; каналы не сужать и не закрывать (Постановление Госстроя № 170, п. 1.7.2). Листы: л. 38 — План вентиляции	акт контрольного обмера; фото с рулеткой и привязкой к стене или углу	Вопроса в реестре нет: Альбом ставит вентиляционные выводы без обмера каналов. Результат принимает: Инженер ОВ
О-4	Все стены квартиры; специализированная организация либо конструктор по проекту дома	Обследование	Какие участки стен несущие: техническое заключение по результатам обследования.	Конструктор или специализированная организация	по заключению организации	Разметка несущих и ненесущих стен на обмерном плане и плане демонтажа; допустимость демонтажа, проёмов и штроб (пока все стены считаются несущими). Листы: л. 21 — План демонтажа и монтажа перегородок	техническое заключение; фото с рулеткой и привязкой к стене или углу	К-3 Результат принимает: Архитектор

Допущения и предложения на листе
Основа листа: размеры сняты с размерных цепочек растрового скана плана заказчика, на объекте не замерены; ступени наружного контура приведены к граням помещений модели (ИЗ-8, К-20, К-21); высота потолка 2700 мм принята, источника нет (К-24); тип дома и перекрытие (монолит, плита 220 мм) приняты, источника нет (К-3); толщины стен приняты (250 и 120 мм), источника нет (К-21); мощность 15 кВт принята, технических условий нет (К-25).
См. лист открытых вопросов (лист 6, запись К-3; лист 7, записи К-20, К-21, К-24, К-25; лист 10, запись ИЗ-8).

Изм.	Кол.уч	Лист	№ док.	Подп.	Дата
Разраб.		Кырлан А.С.			21.10.26
Пров.					
ГИП		Кырлан А.С.			21.10.26
Н. контр.					
Утв.					

ГД-2026-004-АИ

Четырёхкомнатная квартира

Общая площадь 102,67* м² · * размеры со скана, не замерены (реестр — л. 6–11, ИЗ-8, К-20, К-21)

Дизайн-проект интерьера четырёхкомнатной квартиры

Стадия	Лист	Листов
РП	12	124

Задание на контрольный обмер и обследование.
Лист 1 из 5
М б/м

Кырлан Александр Сергеевич

выпуск 05.10.2026 № 7e7a2cd217 · стр. 14 из 168

Задание на контрольный обмер и обследование. Лист 2 из 5

Что замерить, вскрыть и получить до заказа материалов и изделий

Этап 1. До демонтажа (продолжение)

№	Где	Способ	Что сделать	Кто выполняет	Точность	Что пересчитается в альбоме	Чем подтверждается	Закрывает вопросы реестра
О-5	Вся квартира, все 13 помещений; обход по часовой стрелке от входа	Обмер	Контрольный обмер всех помещений: размерные цепочки по каждой стене, общий габарит, толщины стен, диагонали помещений; сверить названия и номера помещений со сканом.	Архитектор	±5 мм; диагонали — разница от 5 мм подписывается	Площади помещений и «Общая площадь» в штампе каждого листа (сейчас расчётные по модели); размеры, по которым заказываются материалы и изделия. Листы: л. 24 — План расстановки мебели л. 2 — Общие данные л. 20 — Обмерный план	акт контрольного обмера	К-4, К-21, К-20 Результат принимает: Дизайнер интерьера, Архитектор
О-6	Кухня, санузлы, гардеробные и помещения со встроенной мебелью	Обмер	Углы и диагонали помещений: кухня, санузлы, гардеробные, помещения со встроенной мебелью. Прямые углы 90° отмечаются на листах только после этого замера.	Архитектор	±5 мм; диагонали — разница от 5 мм подписывается	Отметки прямых углов 90° у кухни, санузлов и гардеробных; площади у скошенных стен (пока условные). Листы: л. 20 — Обмерный план	акт контрольного обмера	К-10 Результат принимает: Архитектор
О-7	Все помещения квартиры	Обмер	Высота потолка в каждом помещении в нескольких точках: центр, углы, у проёмов. Принято 2700 мм: источника в материалах объекта нет.	Архитектор	±5 мм	Вертикальные размеры альбома: развёртки, шкафы и встроенная мебель, плитка, потолки, объёмы работ. Листы: л. 20 — Обмерный план	акт контрольного обмера	К-24 Результат принимает: Архитектор
О-8	Детская 2 (пом. 9), наружная стена В: окно принято по центру наружного участка 8030–10610, привязки 1580…3080 — допущение, не замер	Обмер	Окно Детской 2: положение (привязки к углам эркера), ширина, высота, подоконник.	Архитектор	±5 мм	Положение окна, радиатор под окном, шторы; конфликт со стояками (Кф-1). Листы: л. 20 — Обмерный план	акт контрольного обмера; фото с рулеткой и привязкой к стене или углу	К-1 Результат принимает: Архитектор
О-9	Детская 2 (пом. 9): Ст К1-2*, Ст В1-2*; наличие стояка ГВС, арматуры и счётчиков — по всей квартире	Обмер	Положение стояков Ст К1-2*, Ст В1-2*: привязка осей от граней стен, диаметры, размеры короба и люков. Стояк горячей воды Т3 в данных не задан, на листах ВК принят рядом с Ст В1-2*: выяснить, есть ли он в доме, и где. Отключающая арматура и счётчики воды на вводах: положение, тип, пломбы управляющей компании. Сверить до разметки выводов.	Архитектор	±5 мм	Привязки выводов воды и канализации на планах выводов и разводки; расстояние розеток до стояка; места люков 300 × 400 мм; трассы Т3 и полотенцесушители (водяной или электрический); узлы ввода в спецификации ВК (краны, фильтры, счётчики). Положение стояков, короба и люка; совмещение с проёмом окна 8540–10040, радиатором и шторами; выпуск унитаза П8 (от этого положения 2,4 м). Листы: л. 40 — План выводов сантехники л. 41 — Схема разводки водопровода и канализации л. 20 — Обмерный план	акт контрольного обмера; фото с рулеткой и привязкой к стене или углу	К-15, К-1 Результат принимает: Инженер ВК (вода, канализация), Архитектор
О-10	Гостиная (пом. 11, три ступени вместо скоса) и Гардеробная 1 (пом. 12)	Обмер	Углы и длины скосов наружных стен Гостиной и Гардеробной 1: в натуре стены под 45°, Гардеробная 1 — трапеция 2320/2132/1400 мм вместо прямоугольника 1400×2230 мм в модели. Результат передать отдельным чертежом.	Архитектор	±5 мм; диагонали — разница от 5 мм подписывается	Форма наружных стен и площади Гостиной (по модели 14,55 м² против ≈17 м² по реконструкции контура) и Гардеробной 1; размеры вдоль скоса. Листы: л. 20 — Обмерный план л. 24 — План расстановки мебели	акт контрольного обмера; фото с рулеткой и привязкой к стене или углу	К-5, К-20 Результат принимает: Архитектор
О-11	Гостиная (пом. 11; в примечании проекта «зал»): по скану угол может лежать примерно на 700 мм левее	Обмер	Расстояние от опорной стены до угла помещения «Гостиная»: проверить принятую точку (10670; 3470) мм.	Архитектор	±5 мм	Размеры правой части квартиры: Гостиная, Гардеробная 1, стена Детской 2 со стороны Гостиной; привязки мебели, света и розеток к принятым координатам. Листы: л. 20 — Обмерный план	акт контрольного обмера; фото с рулеткой и привязкой к стене или углу	К-19 Результат принимает: Архитектор

Допущения и предложения на листе

Основа листа: размеры сняты с размерных цепочек растрового скана плана заказчика, на объекте не замерены; ступени наружного контура приведены к граням помещений модели (ИЗ-8, К-20, К-21); высота потолка 2700 мм принята, источника нет (К-24); тип дома и перекрытие (монолит, плита 220 мм) приняты, источника нет (К-3); толщины стен приняты (250 и 120 мм), источника нет (К-21); мощность 15 кВт принята, технических условий нет (К-25).

Знак «*» — принято, не замерено и не подтверждено (замерить на объекте): К-1, К-15: Ст К1-2, Ст В1-2.

См. лист открытых вопросов (лист 6, записи К-1, К-3; лист 7, записи К-15, К-20, К-21, К-24, К-25; лист 10, запись ИЗ-8).

Изм.	Кол.уч	Лист	№ док.	Подп.	Дата
Разраб.		Кырлан А.С.			21.10.26
Пров.					
ГИП		Кырлан А.С.			21.10.26
Н. контр.					
Утв.					

ГД-2026-004-АИ

Четырёхкомнатная квартира

Общая площадь 102,67* м² · * размеры со скана, не замерены (реестр — л. 6–11, ИЗ-8, К-20, К-21)

Дизайн-проект интерьера четырёхкомнатной квартиры

Стадия	Лист	Листов
РП	13	124

Задание на контрольный обмер и обследование.
Лист 2 из 5
М б/м

Кырлан Александр Сергеевич

Задание на контрольный обмер и обследование. Лист 3 из 5

Что замерить, вскрыть и получить до заказа материалов и изделий

Этап 1. До демонтажа (продолжение)

№	Где	Способ	Что сделать	Кто выполняет	Точность	Что пересчитается в альбоме	Чем подтверждается	Закрывает вопросы реестра
О-12	Гостиная (пом. 11), наружная стена В, часть 2: размеры 1500×1600 мм и подоконник 900 мм приняты типовыми	Обмер	Окно Гостиной: положение, ширина, высота, подоконник.	Архитектор	±5 мм	Размеры окна и подоконника на плане (напечатаны как принятые, не замеренные). Листы: л. 20 — Обмерный план	акт контрольного обмера; фото с рулеткой и привязкой к стене или углу	К-22 Результат принимает: Архитектор

Этап 2. После демонтажа, до черновых работ

№	Где	Способ	Что сделать	Кто выполняет	Точность	Что пересчитается в альбоме	Чем подтверждается	Закрывает вопросы реестра
О-13	Зал (пом. 1), Ванная комната (пом. 2), Тёмная комната (пом. 3), Детская 1 (пом. 4), Коридор (пом. 5), Кухня (пом. 6), Прихожая-коридор (пом. 7), Гардеробная 2 (пом. 8), Детская 2 (пом. 9), Санузел (пом. 10), Гостиная (пом. 11), Гардеробная 1 (пом. 12), Балкон 1 (пом. 13)	Обмер	Нивелировка плиты перекрытия и существующего пола после демонтажа покрытий: отметки в углах и по сетке, перепады по помещению, уклоны, отметки порогов (чистый пол в мокрых зонах принят -30 мм, -15 мм, 0 мм). Принятая толщина стяжки 53 мм, 55 мм и отметка чистого пола — расчётные, не от замера плиты.	Архитектор	±5 мм по отметке; ровность просвет под 2-метровой рейкой, горизонталь против 0,2 % длины помещения	Толщина стяжки и отметка чистого пола; уклоны к трапам и пороги; выпуски К1 относительно чистого пола (план разводки); объёмы стяжки и смеси в ВОР и спецификации. Листы: л. 49, 53, 54 — План полов л. 41 — Схема разводки водопровода и канализации	акт контрольного обмера	Вопроса в реестре нет: Альбом принимает отметки плиты и толщину пирога пола без нивелировки. Результат принимает: Отделочник
О-14	Зал (пом. 1), Ванная комната (пом. 2), Тёмная комната (пом. 3), Детская 1 (пом. 4), Коридор (пом. 5), Кухня (пом. 6), Прихожая-коридор (пом. 7), Гардеробная 2 (пом. 8), Детская 2 (пом. 9), Санузел (пом. 10), Гостиная (пом. 11), Гардеробная 1 (пом. 12), Балкон 1 (пом. 13)	Обмер	Вертикаль и плоскостность стен: отклонение от вертикали по высоте стены (отвес или лазерный уровень), просвет под правилом 2 м, кривизна углов. Нужно там, где от стены зависит изделие: облицовка плиткой (пом. 2, 10), штукатурка и окраска (пом. 1, 2, 3, 4, 5, 6, 7, 8, 9, 10, 11, 12, 13), встроенная мебель и кухня (пом. 3, 4, 5, 6, 7, 8, 9, 12, 13).	Архитектор	до 1 мм на 2 м (правило и клиновой щуп); вертикаль — мм на высоту стены, отклонения подписываются на плане	Толщина штукатурки и расход смеси в ВОР и спецификации; раскладка плитки (подрезка у стен); зазоры и крепление встроенной мебели и кухни. Листы: л. 49–52 — Раскладка плитки л. 55–57 — Ведомость отделки помещений	акт контрольного обмера	Вопроса в реестре нет: Альбом принимает стены ровными и вертикальными без замера. Результат принимает: Отделочник
О-15	Ванная комната (стена Б, модуль М8); Кухня (стена А, модули М24–М26); Гардеробная 2 (стена В, модуль М33)	Вскрытие	Определить материал и толщину стены в местах установки навесных модулей: вскрыть основание после снятия старой отделки.	Бригада по указанию прораба	толщина ±5 мм; материал — по вскрытию	Крепёж навесных модулей: анкер по бетону или закладная в ГКЛ; материал основания в данных проекта (сейчас не указан); монтажные схемы кухни и шкафов. Листы: л. 82 — Кухня (пом. 6). Монтажная схема л. 84 — Кухня (пом. 6). Монтажная схема л. 85–87 — Шкафы. Монтажная схема	фото с рулеткой и привязкой к стене или углу; акт контрольного обмера	К-14 Результат принимает: Мебельщик

Допущения и предложения на листе

Основа листа: размеры сняты с размерных цепочек растрового скана плана заказчика, на объекте не замерены; ступени наружного контура приведены к граням помещений модели (ИЗ-8, К-20, К-21); высота потолка 2700 мм принята, источника нет (К-24); тип дома и перекрытие (монолит, плита 220 мм) приняты, источника нет (К-3); толщины стен приняты (250 и 120 мм), источника нет (К-21); мощность 15 кВт принята, технических условий нет (К-25).

См. лист открытых вопросов (лист 6, запись К-3; лист 7, записи К-20, К-21, К-24, К-25; лист 10, запись ИЗ-8).

Изм.	Кол.уч	Лист	№ док.	Подп.	Дата
Разраб.		Кырлан А.С.			21.10.26
Пров.					
ГИП		Кырлан А.С.			21.10.26
Н. контр.					
Утв.					

ГД-2026-004-АИ

Четырёхкомнатная квартира

Общая площадь 102,67* м² · * размеры со скана, не замерены (реестр — л. 6–11, ИЗ-8, К-20, К-21)

Дизайн-проект интерьера четырёхкомнатной квартиры

Стадия	Лист	Листов
РП	14	124

Задание на контрольный обмер и обследование.
Лист 3 из 5
М б/м

Кырлан Александр Сергеевич

выпуск 05.10.2026 № 7e7a2cd217 · стр. 16 из 168

Задание на контрольный обмер и обследование. Лист 4 из 5

Что замерить, вскрыть и получить до заказа материалов и изделий

Этап 3. После черновых работ, до чистового пола

№	Где	Способ	Что сделать	Кто выполняет	Точность	Что пересчитается в альбоме	Чем подтверждается	Закрывает вопросы реестра
О-16	Кухня, Ванная комната, Санузел, Гардеробная 1 и 2	Обмер	Габариты кухни и помещений со встроенной мебелью по готовым стенам: размеры после штукатурки и выравнивания.	Архитектор	±5 мм	Размеры встроенной мебели и кухни; монтажные схемы гарнитура и шкафов. Листы: л. 20 — Обмерный план	акт контрольного обмера	К-10 Результат принимает: Архитектор
О-17	Детская 2 (пом. 9): М36*	Обмер	Положение и габариты по готовым стенам и по месту: М36* (стол письменный у стены б). Принято по проекту, подтвердить на объекте перед заказом и монтажом. Основание допущения: положение и размеры стола утверждены автором (ИЗ-1); боковой свет от окна справа принят допустимым, рабочая рука того, кто сидит за столом, не известна (К-13).	Архитектор	±5 мм	Габариты и привязки предметов на планах расстановки и развёртках; выводы электрики и ВК, если они привязаны к предмету. Листы: л. 24 — План расстановки мебели	акт контрольного обмера	К-13 Результат принимает: Дизайнер интерьера

Документы и данные закупки (не на объекте)

№	У кого, откуда	Способ	Что получить	К какому сроку	Что пересчитается в альбоме	Чем подтверждается	Закрывает вопросы реестра
О-18	Заказчик (документы на квартиру и дом)	Документ	План БТИ и проект дома: тип и серия дома, материал и толщина перекрытия (принято: монолитная плита 220 мм), какие стены несущие.	До любого демонтажа и штробления в стенах	Тип дома и конструкция перекрытия в данных объекта; разметка несущих и ненесущих стен на обмерном плане и плане демонтажа; допустимость демонтажа, проёмов и штроб (пока все стены считаются несущими). Листы: л. 21 — План демонтажа и монтажа перегородок	копия документа	К-3 Результат принимает: Архитектор
О-19	Поставщик или изготовитель вытяжки; модель пока не выбрана	Закупка	Паспорт выбранной модели вытяжки: допустимая высота низа над электрической варочной панелью.	До заказа модулей М24–М26	Отметка модуля М25 и соседних М24, М26; расстояние от варочной панели до вытяжки (сейчас 610 мм при фартуке 650 мм). Листы: л. 81 — Кухня (пом. 6). Развёртка гарнитура	паспорт изделия или партии	К-18 Результат принимает: Мебельщик
О-20	Заказчик; организация, выдавшая технические условия	Документ	Технические условия на присоединение: разрешённая мощность (принято 15 кВт, расчётная 11,2 кВт); источника в материалах объекта нет.	До утверждения однолинейной схемы щита	Однолинейная схема щита: вводной аппарат и группы; сверка расчётной мощности 11,2 кВт с разрешённой. Листы: л. 34, 35 — Однолинейная схема щита	копия документа	К-25 Результат принимает: Инженер-электрик
О-21	Образцы и паспорта изделий от поставщика; код изделия производителя	Закупка	Артикулы изделий отделки: инженерная доска 14/4 мм (дуб натуральный брашированный, масло-воск); керамогранит пола матовый 600 × 600 × 10 мм, R10 (тон J484 — пом. 2, 10; тон V486 — пом. 5, 7) и R11 (тон V486 — пом. 13); керамогранит стен матовый 600 × 600 × 9 мм, тон F497 (пом. 2, 10, фартук кухни пом. 6); плинтус МДФ под окраску 80 × 16 мм; плинтус из керамогранита пола, подрезка 80 мм, кромка с запилом 45° (пом. 13); интерьерная краска акцентных стен, класс 2 по EN 13300, база С (пом. 1, 11).	До заказа материалов	Ведомость отделки помещений, спецификации материалов, количество упаковок и смета: подсчёт по номинальным размерам заменить подсчётом по выбранным изделиям. Листы: л. 49 — Раскладка плитки. Планы полов л. 50 — Раскладка плитки. Фартук кухни л. 51 — Раскладка плитки. Ванная комната. Развёртки стен л. 52 — Раскладка плитки. Санузел. Развёртки стен л. 53 — План полов л. 55–57 — Ведомость отделки помещений л. 58, 59 — Колерная карта л. 60, 61 — Спецификация отделочных материалов л. 89 — Реестр марок отделки и позиций альбома л. 121, 122 — Спецификация материалов л. 123, 124 — Смета ориентировочная	паспорт изделия или партии; образец	К-26 Результат принимает: Отделочник

Допущения и предложения на листе

Основа листа: размеры сняты с размерных цепочек растрового скана плана заказчика, на объекте не замерены; ступени наружного контура приведены к граням помещений модели (ИЗ-8, К-20, К-21); высота потолка 2700 мм принята, источника нет (К-24); тип дома и перекрытие (монолит, плита 220 мм) приняты, источника нет (К-3); толщины стен приняты (250 и 120 мм), источника нет (К-21); мощность 15 кВт принята, технических условий нет (К-25).

Знак «*» — принято, не замерено и не подтверждено (замерить на объекте): ИЗ-1, К-13: М36 — положение и размеры стола утверждены автором (ИЗ-1); боковой свет от окна справа принят допустимым, рабочая рука того, кто сидит за столом, не известна (К-13).

См. лист открытых вопросов (лист 6, записи К-3, К-13; лист 7, записи К-20, К-21, К-24, К-25; лист 9, запись ИЗ-1; лист 10, запись ИЗ-8).

Изм.	Кол.уч	Лист	№ док.	Подп.	Дата
Разраб.		Кырлан А.С.			21.10.26
Пров.					
ГИП		Кырлан А.С.			21.10.26
Н. контр.					
Утв.					

ГД-2026-004-АИ

Четырёхкомнатная квартира

Общая площадь 102,67* м² · * размеры со скана, не замерены (реестр — л. 6–11, ИЗ-8, К-20, К-21)

Дизайн-проект интерьера четырёхкомнатной квартиры

Стадия	Лист	Листов
РП	15	124

Задание на контрольный обмер и обследование.
Лист 4 из 5
М б/м

Кырлан Александр Сергеевич

выпуск 05.10.2026 № 7e7a2cd217 · стр. 17 из 168

Задание на контрольный обмер и обследование. Лист 5 из 5

ПРЕДВАРИТЕЛЬНО · не для производства работ · открыто пунктов: 30 (реестр — л. 6–11)

Что замерить, вскрыть и получить до заказа материалов и изделий

Документы и данные закупки (не на объекте) (продолжение)

№	У кого, откуда	Способ	Что получить	К какому сроку	Что пересчитается в альбоме	Чем подтверждается	Закрывает вопросы реестра
О-22	Поставщик или изготовитель техники; паспорт и монтажная схема выбранной модели	Закупка	Модели и монтажные схемы встраиваемой техники: холодильник (М20), духовой шкаф (М22), посудомоечная машина (М27) габариты ниши, вентзазоры, высота цоколя и решётки, подключение.	До заказа модулей кухни	Размеры ниш модулей М20, М22, М27; вентиляция в цоколе и за корпусом; точки подключения техники на листе кухни. Листы: л. 81 — Кухня (пом. 6). Развёртка гарнитура л. 82 — Кухня (пом. 6). Монтажная схема	паспорт изделия или партии	К-27 Результат принимает: Мебельщик

Примечания

1. Подтверждение: акт контрольного обмера (дата, кто присутствовал, прибор, перечень промеров с результатами, подписи присутствующих); к акту — фото вскрытий и узлов и техническое заключение организации, выполнившей обследование.
2. Номера листов — по ведомости рабочих чертежей комплекта (лист «Общие данные»).
3. Пункт исключается из задания при следующем выпуске, когда акт подписан, значение внесено в проект и листы перевыпущены; знак «*» у величины снимается только замером.

Допущения и предложения на листе

Основа листа: размеры сняты с размерных цепочек растрового скана плана заказчика, на объекте не замерены; ступени наружного контура приведены к граням помещений модели (ИЗ-8, К-20, К-21); высота потолка 2700 мм принята, источника нет (К-24); тип дома и перекрытие (монолит, плита 220 мм) приняты, источника нет (К-3); толщины стен приняты (250 и 120 мм), источника нет (К-21); мощность 15 кВт принята, технических условий нет (К-25).
См. лист открытых вопросов (лист 6, запись К-3; лист 7, записи К-20, К-21, К-24, К-25; лист 10, запись ИЗ-8).

Изм.	Кол.уч	Лист	№ док.	Подп.	Дата
Разраб.		Кырлан А.С.			21.10.26
Пров.					
ГИП		Кырлан А.С.			21.10.26
Н. контр.					
Утв.					

ГД-2026-004-АИ

Четырёхкомнатная квартира

Общая площадь 102,67* м² · * размеры со скана, не замерены (реестр — л. 6–11, ИЗ-8, К-20, К-21)

Дизайн-проект интерьера четырёхкомнатной квартиры

Стадия	Лист	Листов
РП	16	124

Задание на контрольный обмер и обследование.
Лист 5 из 5
М б/м

Кырлан Александр Сергеевич

выпуск 05.10.2026 № 7e7a2cd217 · стр. 18 из 168

График закупок и работ. Лист 1 из 3

Что заказывать и когда не раньше чего: относительный порядок без дат; срок поставки — из данных или «уточняется у поставщика»

Лист не содержит дат: контрольного обмера, подписанных решений автора и договоров ещё нет, и любая дата была бы выдумана. Вместо календаря — порядок и условия: замер → решение и выбор изделия → заказ → срок поставки → работа, которую позиция блокирует.
Срок поставки печатается как срок, только если он задан в данных позиции. Нет — «срок уточняется у поставщика» и ссылка на вопрос реестра о сроках; типовой диапазон практики стоит рядом как ориентир и заказывать по нему нельзя. Номера З-N и Р-N — строки этого листа, К-N — записи реестра открытых вопросов, О-N — позиции задания на контрольный обмер.

Закупки: что заказывается, от чего зависит заказ и какую работу блокирует

№	Позиция и где	1. Замер до заказа	2. Решение, выбор изделия, паспорт	3. Условие заказа	4. Срок поставки	5. Блокирует работу	Закрывает вопросы реестра
З-1	Кухонный гарнитур по проекту кухни: модули М20, М21, М22, М23, М24, М25, М26, М28 пом. 6			После 1 и 2 и после получения срока у поставщика (вопроса о сроках нет); дата заказа — когда срок известен, не позднее чем за срок до начала Р-15.	срок уточняется у поставщика Ориентир практики (не срок поставщика): 4–8 нед. от замера	Р-15 «кухня и мебель»: замер кухни — по готовым стенам после штукатурки или плитки, до чистового пола; производство идёт параллельно со стяжкой и отделкой	
З-2	Встраиваемая техника кухни: М20 холодильник, М22 oven, М25 вытяжка, М27 посудомоечная машина пом. 6		О-19: Паспорт выбранной модели вытяжки: допустимая высота низа над электрической варочной панелью. (К-18); до заказа модулей М24–М26 О-22: Модели и монтажные схемы встраиваемой техники: холодильник (М20), духовой шкаф (М22), посудомоечная машина (М27) — габариты ниши, вентзазоры, высота цоколя и решётки, подключение. (К-27); до заказа модулей кухни	После 1 и 2 и после получения срока у поставщика (вопроса о сроках нет); дата заказа — когда срок известен, не позднее чем за срок до начала Р-15.	срок уточняется у поставщика	Р-15 «кухня и мебель»: паспорта и монтажные схемы — до изготовления модулей кухни: нишу и вентзазоры задаёт модель, а не типовая схема 60 см	К-18, К-27
З-3	Стиральная машина: П4 (вертикальная загрузка 400 × 600 мм — условие закупки) пом. 2			После 1 и 2 и после получения срока у поставщика (вопроса о сроках нет); дата заказа — когда срок известен, не позднее чем за срок до начала Р-4.	срок уточняется у поставщика	Р-4 «черновая сантехника»: габарит и подводка — до закрытия люка и разводки	
З-4	Сантехнические приборы и инсталляции: П1, П2, П3, П6, П8, П9 пом. 2, 6, 10	О-9: обмер: Детская 2 (пом. 9): Ст К1-2*, Ст В1-2; наличие стояка ГВС, арматуры и счётчиков — по всей квартире (К-15, К-1) О-2: обмер: Зал (пом. 1), Детская 1 (пом. 4), Кухня (пом. 6), Детская 2 (пом. 9), Гостиная (пом. 11); у окон		После 1 и 2 и после получения срока у поставщика (вопроса о сроках нет); дата заказа — когда срок известен, не позднее чем за срок до начала Р-4.	срок уточняется у поставщика	Р-4 «черновая сантехника»: инсталляцию ставят до обшивки ГКЛВ и до гидроизоляции стены	К-1, К-15
З-5	Керамогранит и плитка: 3 поз. по артикулу и формату, 54,55 м² по раскладке пом. 2, 5, 6, 7, 10	О-13: обмер: Зал (пом. 1), Ванная комната (пом. 2), Тёмная комната (пом. 3), Детская 1 (пом. 4), Коридор (пом. 5), Кухня (пом. 6), Прихожая-коридор (пом. 7), Гардеробная 2 (пом. 8), Детская 2 (пом. 9), Санузел (пом. 10), Гостиная (пом. 11), Гардеробная 1 (пом. 12), Балкон 1 (пом. 13) О-14: обмер: Зал (пом. 1), Ванная комната (пом. 2), Тёмная комната (пом. 3), Детская 1 (пом. 4), Коридор (пом. 5), Кухня (пом. 6), Прихожая-коридор (пом. 7), Гардеробная 2 (пом. 8), Детская 2 (пом. 9), Санузел (пом. 10), Гостиная (пом. 11), Гардеробная 1 (пом. 12), Балкон 1 (пом. 13)	О-21: Артикулы изделий отделки: инженерная доска 14/4 мм (дуб натуральный брашированный, масло-воск); керамогранит пола матовый 600 × 600 × 10 мм, R10 (тон J484 — пом. (К-26); до заказа материалов	После 1 и 2 и после получения срока у поставщика (вопроса о сроках нет); дата заказа — когда срок известен, не позднее чем за срок до начала Р-9.	срок уточняется у поставщика	Р-9 «плитка»: калибр партии измеряют до раскладки, раскладку пересчитывают до заказа	К-26

Допущения и предложения на листе
Основа листа: размеры сняты с размерных цепочек растрового скана плана заказчика, на объекте не замерены; ступени наружного контура приведены к граням помещений модели (ИЗ-8, К-20, К-21); высота потолка 2700 мм принята, источника нет (К-24); тип дома и перекрытие (монолит, плита 220 мм) приняты, источника нет (К-3); толщины стен приняты (250 и 120 мм), источника нет (К-21); мощность 15 кВт принята, технических условий нет (К-25).
Знак «*» — принято, не замерено и не подтверждено (замерить на объекте): К-1, К-15: Ст К1-2.
См. лист открытых вопросов (лист 6, записи К-1, К-3; лист 7, записи К-15, К-20, К-21, К-24, К-25; лист 10, запись ИЗ-8).

Изм.	Кол.уч	Лист	№ док.	Подп.	Дата
Разраб.		Кырлан А.С.			21.10.26
Пров.					
ГИП		Кырлан А.С.			21.10.26
Н. контр.					
Утв.					

ГД-2026-004-АИ

Четырёхкомнатная квартира

Общая площадь 102,67* м² · * размеры со скана, не замерены (реестр — л. 6–11, ИЗ-8, К-20, К-21)

Дизайн-проект интерьера четырёхкомнатной квартиры

Стадия	Лист	Листов
РП	17	124

График закупок и работ. Лист 1 из 3

М б/м

Кырлан Александр Сергеевич

выпуск 05.10.2026 № 7e7a2cd217 · стр. 19 из 168

График закупок и работ. Лист 2 из 3

Что заказывать и когда не раньше чего: относительный порядок без дат; срок поставки — из данных или «уточняется у поставщика»

Закупки: что заказывается, от чего зависит заказ и какую работу блокирует (продолжение)

№	Позиция и где	1. Замер до заказа	2. Решение, выбор изделия, паспорт	3. Условие заказа	4. Срок поставки	5. Блокирует работу	Закрывает вопросы реестра
З-6	Покрытие пола (доска) и плинтус: пом. 1, 3, 4, 6, 8, 9, 11, 12 пом. 1, 3, 4, 6, 8, 9, 11, 12	О-13: обмер: Зал (пом. 1), Ванная комната (пом. 2), Тёмная комната (пом. 3), Детская 1 (пом. 4), Коридор (пом. 5), Кухня (пом. 6), Прихожая-коридор (пом. 7), Гардеробная 2 (пом. 8), Детская 2 (пом. 9), Санузел (пом. 10), Гостиная (пом. 11), Гардеробная 1 (пом. 12), Балкон 1 (пом. 13)	О-21: Артикулы изделий отделки: инженерная доска 14/4 мм (дуб натуральный брашированный, масло-воск); керамогранит пола матовый 600 × 600 × 10 мм, R10 (тон J484 — пом. (К-26); до заказа материалов	После 1 и 2 и после получения срока у поставщика (вопроса о сроках нет); дата заказа — когда срок известен, не позднее чем за срок до начала Р-12.	срок уточняется у поставщика	Р-12 «чистовые полы»: артикул и партия — до заказа; доску привозят к чистовым полам	К-26
З-7	Встроенная мебель по замеру цеха: М9, М10, М16, М19, М29, М32, М33, М35, М39, М41, М42 пом. 3, 4, 5, 7, 8, 9, 12, 13	О-17: обмер: Детская 2 (пом. 9): М36* (К-13) О-5: обмер: Вся квартира, все 13 помещений; обход по часовой стрелке от входа (К-4, К-21, К-20)		После 1 и 2 и после получения срока у поставщика (вопроса о сроках нет); дата заказа — когда срок известен, не позднее чем за срок до начала Р-15.	срок уточняется у поставщика Ориентир практики (не срок поставщика): 4–8 нед. от замера	Р-15 «кухня и мебель»: цех замеряет по готовым стенам; производство 4–8 недель идёт параллельно с отделкой	К-4, К-13, К-20, К-21

Работы: порядок и что не даёт начать

№	Работа (стадия технологической последовательности)	После	Что должно быть к началу: условия и закупки	Не начинать, пока открыто в реестре
Р-1	Демонтаж покрытий, отделки стен и потолков, дверных блоков и приборов; конструкции, стены и перегородки не трогать до технического заключения (стадия 1)		до начала: запрошены документы на дом и БТИ; контрольный обмер до демонтажа (что видно) сделан	
Р-2	Контрольный обмер на голых стенах и обследование (задание — лист «Задание на контрольный обмер») (стадия 2)	Р-1	после снятия отделки: видны стояки, каналы, щиток, толщины стен; до заказа всего, что делают по размеру	
Р-3	Черновая электрика: штробы, короба, гофра, подрозетники, щит (стадия 4)	Р-2	до начала: план электрики с высотами утверждён; штробы в стенах — только после технического заключения; мебель расставлена	К-25: Разрешённая мощность 15 кВт принята, технических условий в материалах объекта нет; расчётная мощность 11,2 кВт.
Р-4	Черновая сантехника и вентиляция: разводка, выводы, инсталляции, короба стояков (стадия 5)	Р-2	до начала: положение стояков замерено; модели инсталляций и машины выбраны (габариты рамы, подводка); инсталляцию ставят до обшивки ГКЛВ и до гидроизоляции Закупки к началу: З-3 (стиральная машина), З-4 (сантехника)	К-1: Окно детской 2 (поз. К-15: Стояки Ст К1-2* и Ст В1-2* (в данных (9400; 6300) и (9560; 6300), короб и люк) попадают в проём окна Детской 2 по стене В (8540–10040): совместить с радиатором под окном и шторами нельзя.
Р-5	Коробки скрытых дверей, затем штукатурка стен и откосов (стадия 6)	Р-2, Р-3, Р-4	до начала: электрика и сантехника смонтированы, штробы заделаны; коробки скрытых дверей установлены до штукатурки (поэтому заказ дверей — раньше работы)	
Р-6	Стяжка пола и тёплый пол (стадия 7)	Р-5	до начала: штукатурка сделана; трубы под стяжкой приняты; нивелировка плиты выполнена	
Р-7	Гидроизоляция санузлов и тест проливом (стадия 8)	Р-6	до начала: стяжка набрала прочность и сухая по инструкции гидроизоляции; выводы стоят на проектных отметках	
Р-8	ГКЛ: короба инсталляции и стояков, ниши, потолки (стадия 9)	Р-3, Р-4	до начала: черновые сети в зоне коробов приняты; закладные под тяжёлое и карнизы стоят; светильники выбраны (вырезы)	
Р-9	Плитка и керамогранит: стены, затем пол; фартук (стадия 10)	Р-6, Р-7, Р-8	до начала: гидроизоляция принята; плитка выбрана, калибр партии измерен, раскладка пересчитана и подписана Закупки к началу: З-5 (плитка)	К-26: Артикулы изделий отделки не выбраны.
Р-10	Шпаклёвка стен и потолков под окраску (стадия 11)	Р-5, Р-8, Р-9	до начала: плитка готова (грязные работы закончены); штукатурка и ГКЛ сухие	

Допущения и предложения на листе

Основа листа: размеры сняты с размерных цепочек растрового скана плана заказчика, на объекте не замерены; ступени наружного контура приведены к граням помещений модели (ИЗ-8, К-20, К-21); высота потолка 2700 мм принята, источника нет (К-24); тип дома и перекрытие (монолит, плита 220 мм) приняты, источника нет (К-3); толщины стен приняты (250 и 120 мм), источника нет (К-21); мощность 15 кВт принята, технических условий нет (К-25).

Знак «*» — принято, не замерено и не подтверждено (замерить на объекте): ИЗ-1, К-13: М36 — положение и размеры стола утверждены автором (ИЗ-1); боковой свет от окна справа принят допустимым, рабочая рука того, кто сидит за столом, не известна (К-13); К-1, К-15: Ст К1-2, Ст В1-2.

См. лист открытых вопросов (лист 6, записи К-1, К-3, К-13; лист 7, записи К-15, К-20, К-21, К-24, К-25; лист 9, запись ИЗ-1; лист 10, запись ИЗ-8).

Изм.	Кол.уч	Лист	№ док.	Подп.	Дата
Разраб.		Кырлан А.С.			21.10.26
Пров.					
ГИП		Кырлан А.С.			21.10.26
Н. контр.					
Утв.					

ГД-2026-004-АИ

Четырёхкомнатная квартира

Общая площадь 102,67* м² · * размеры со скана, не замерены (реестр — л. 6–11, ИЗ-8, К-20, К-21)

Дизайн-проект интерьера четырёхкомнатной квартиры

Стадия	Лист	Листов
РП	18	124

График закупок и работ. Лист 2 из 3

М б/м

Кырлан Александр Сергеевич

выпуск 05.10.2026 № 7e7a2cd217 · стр. 20 из 168

График закупок и работ. Лист 3 из 3

Что заказывать и когда не раньше чего: относительный порядок без дат; срок поставки — из данных или «уточняется у поставщика»

Работы: порядок и что не даёт начать (продолжение)

№	Работа (стадия технологической последовательности)	После	Что должно быть к началу: условия и закупки	Не начинать, пока открыто в реестре
Р-11	Окраска стен, потолков, откосов (стадия 13)	Р-10	до начала: шпаклёвка отшлифована и огрунтована; выкрасы утверждены, колеровка одной партией	
Р-12	Чистовые полы: инженерная доска (стадия 14)	Р-9, Р-11	до начала: влажность основания в норме, мокрые работы закончены; доска выбрана и привезена Закупки к началу: З-6 (доска и плинтус)	К-26: Артикулы изделий отделки не выбраны.
Р-13	Полотна межкомнатных дверей, плинтусы, пороги (стадия 15)	Р-11, Р-12	до начала: чистовой пол уложен; полотна скрытых дверей — после чистовой отделки стен	
Р-14	Чистовая электрика и сантехника: механизмы, светильники, смесители, приборы (стадия 16)	Р-11, Р-13	до начала: отделка готова; механизмы, светильники и приборы выбраны и привезены	
Р-15	Кухня, встроенная и корпусная мебель, бытовая техника (стадия 17)	Р-13, Р-14	до начала: чистовая сантехника и электрика подведены к местам мебели; замер кухни снят по готовым стенам (после штукатурки или плитки, до чистового пола) Закупки к началу: З-1 (кухонный гарнитур), З-2 (техника кухни), З-7 (мебель по замеру)	К-4: Гостиная (поз. К-13: Детская 2: рабочий стол М36* у стены Б получает боковой свет от окна справа от сидящего; для правши лучше свет слева — подтвердить, кто сидит за столом (правша или левша), иначе решить зеркальной расстановкой (нужен перенос двери) либо второй лампой слева. К-18: Вытяжка М25 встроена в навесной модуль на отметке 1550 мм: её низ над электрической варочной панелью 610 мм, а фартук 650 мм при практике 450–600 мм. К-20: Наружные скошенные стены (в натуре под 45°) заменены на планах ступенями: движок описывает только ортогональную геометрию. К-21: Все размеры сняты с размерных цепочек растрового скана заказчика, контрольного обмера нет. К-27: Модели встраиваемой техники кухни не выбраны: холодильник (М20), духовой шкаф (М22) и посудомоечная машина (М27) заданы описанием «аналог по характеристикам» — без производителя, серии и кода.
Р-16	Сдача: осмотр по чек-листу, дефектная ведомость, устранение замечаний (стадия 18)	Р-14, Р-15	до начала: всё смонтировано; акты скрытых работ подписаны	

Примечания

1. Порядок работ — стадии технологической последовательности из 16 позиций, присутствующих в этом проекте (по строкам ведомости объёмов); остальные стадии таблицы knowledge/remont-tehnologiya.md в проекте не встречаются. Длительности работ не печатаются: их нет ни в данных, ни в нормах для этого объекта.
2. Типовые сроки — ориентир практики, не срок поставщика: скрытые двери — короб около 10 дн., полотно под покраску до 3 нед., шпон 4–5 нед., в среднем около 30 дн. (knowledge/workers/foreman.md, п. 2.4 (profil-doors)); кухня и корпусная мебель — 4–8 недель от замера (knowledge/remont-tehnologiya.md, разд. 2; knowledge/workers/foreman.md, п. 2.4). Заказ по ориентиру не назначается: срок получают у поставщика (вопрос реестра), после чего заказ планируют «не позднее чем за срок до начала работы».
3. Условия заказа берутся из реестра открытых вопросов и задания на контрольный обмер: позиция заказывается, когда закрыты замер (графа 1) и решение (графа 2). Закрывать их может только факт или решение автора с подписью; снять строку с листа можно только закрыв запись реестра.
4. Заказ по размеру до контрольного обмера не делают: двери, кухня и встроенная мебель зависят от обмера (К-11, К-13); скрытые двери, кроме того, зависят от решения по нише санузла 2 (проём Д-5 в перегородке П-1).
5. Номера листов — по ведомости рабочих чертежей комплекта (лист «Общие данные»).

Допущения и предложения на листе

Основа листа: размеры сняты с размерных цепочек растрового скана плана заказчика, на объекте не замерены; ступени наружного контура приведены к граням помещений модели (ИЗ-8, К-20, К-21); высота потолка 2700 мм принята, источника нет (К-24); тип дома и перекрытие (монолит, плита 220 мм) приняты, источника нет (К-3); толщины стен приняты (250 и 120 мм), источника нет (К-21); мощность 15 кВт принята, технических условий нет (К-25).

Знак «*» — принято, не замерено и не подтверждено (замерить на объекте): ИЗ-1, К-13: М36 — положение и размеры стола утверждены автором (ИЗ-1); боковой свет от окна справа принят допустимым, рабочая рука того, кто сидит за столом, не известна (К-13).

См. лист открытых вопросов (лист 6, записи К-3, К-13; лист 7, записи К-20, К-21, К-24, К-25; лист 9, запись ИЗ-1; лист 10, запись ИЗ-8).

Изм.	Кол.уч	Лист	№ док.	Подп.	Дата
Разраб.		Кырлан А.С.			21.10.26
Пров.					
ГИП		Кырлан А.С.			21.10.26
Н. контр.					
Утв.					

ГД-2026-004-АИ

Четырёхкомнатная квартира

Общая площадь 102,67* м² · * размеры со скана, не замерены (реестр — л. 6–11, ИЗ-8, К-20, К-21)

Дизайн-проект интерьера четырёхкомнатной квартиры

Стадия	Лист	Листов
РП	19	124

График закупок и работ. Лист 3 из 3

М б/м

Кырлан Александр Сергеевич

выпуск 05.10.2026 № 7e7a2cd217 · стр. 21 из 168

01

Архитектурные решения

Кырлан Александр Сергеевич

выпуск 05.10.2026 № 7e7a2cd217 · стр. 22 из 168

Обмерный план

Существующее положение · размеры в мм · отметки от чистого пола

ПРЕДВАРИТЕЛЬНО · не для производства работ · открыто пунктов: 30 (реестр — л. 6–11)

Отметки по высоте

±0,000	чистый пол пом. 1, 3–9, 11, 12; отсчёт высот
−0,015	чистый пол пом. 2, 10, ниже на 15 мм
−0,030	чистый пол пом. 13, ниже на 30 мм
−0,170*	верх плиты — расчёт, не замер (задание на обмер)
сущ. пол	снимается до плиты; не замерен (задание на обмер)

Принято, не определено или спорно

полностью — листы 6–11

К-5 — Гардеробная 1 (поз. 12) в натуре трапеция 2320/2132/1400, в модели прямоугольник той же площади: нужен контрольный обмер углов

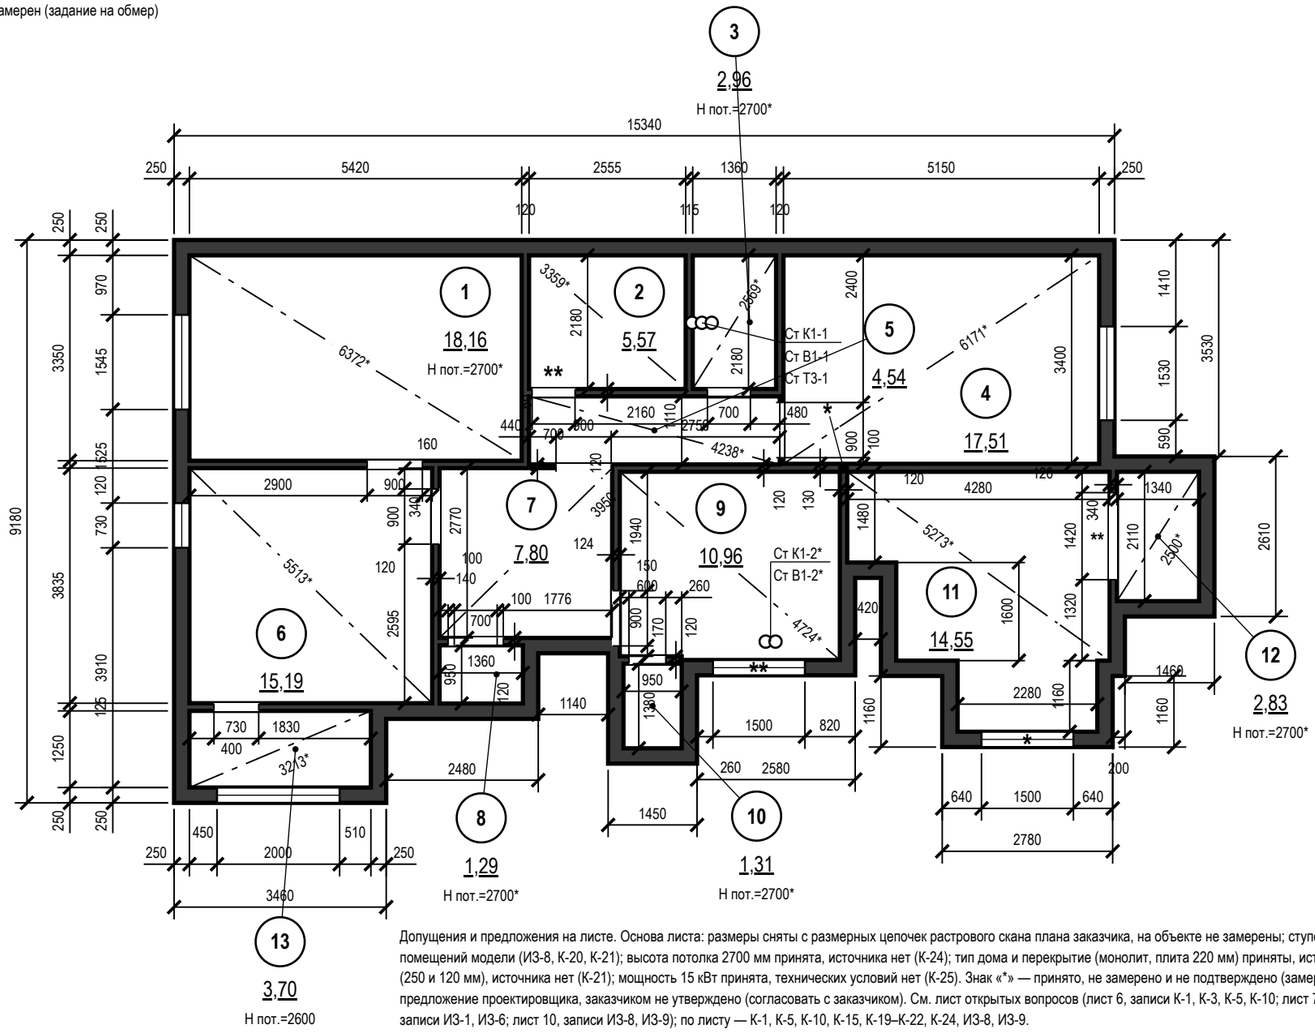

Экспликация помещений

№	Наименование	Площадь, м²
1	Зал	18,16
2	Ванная комната	5,57
3	Тёмная комната	2,96
4	Детская 1	17,51
5	Коридор	4,54
6	Кухня	15,19
7	Прихожая-коридор	7,80
8	Гардеробная 2	1,29
9	Детская 2	10,96
10	Санузел	1,31
11	Гостиная	14,55
12	Гардеробная 1	2,83
13	Балкон 1 *	3,70
	Итого (общая площадь)	**102,67**

Условные обозначения

- существующие стены (сечение)
- окно (рама, остекление)
- проём существующий, без заполнения (откосы)
- стояк: К1 — канализация, В1 — ХВС, Т3 — ГВС
- ** — «**» — предложение проектировщика, заказчиком не утверждено
- диагональ помещения — контроль прямоугольности
- 1 — номер помещения, площадь м²
- * — «*» — принято, не замерено и не подтверждено

Допущения и предложения на листе. Основа листа: размеры сняты с размерных цепочек растрового скана плана заказчика, на объекте не замерены; ступени наружного контура приведены к граням помещений модели (ИЗ-8, К-20, К-21); высота потолка 2700 мм принята, источника нет (К-24); тип дома и перекрытие (монолит, плита 220 мм) приняты, источника нет (К-3); толщины стен приняты (250 и 120 мм), источника нет (К-21); мощность 15 кВт принята, технических условий нет (К-25). Знак «*» — принято, не замерено и не подтверждено (замерить на объекте). Знак «**» — предложение проектировщика, заказчиком не утверждено (согласовать с заказчиком). См. лист открытых вопросов (лист 6, записи К-1, К-3, К-5, К-10; лист 7, записи К-15, К-19–К-22, К-24, К-25; лист 9, записи ИЗ-1, ИЗ-6; лист 10, записи ИЗ-8, ИЗ-9); по листу — К-1, К-5, К-10, К-15, К-19–К-22, К-24, ИЗ-8, ИЗ-9.

Примечания

1. Размеры — в мм по чистым поверхностям стен до отделки (по плану заказчика); площади — в м² по тем же размерам. До начала работ выполнить контрольный обмер.
2. Источник плана — допущение, не замер: растровый скан плана заказчика, размеры сняты с размерных цепочек, на объекте не замерены; скошенные стены приведены к ступеням (на плане не натура), углы 90° и диагонали не подтверждены; привязка угла зала принята (знак «*»): по пиксельной привязке скана он может быть на ~700 мм левее; названия и номера помещений со сканом не сверены. Реестр: листы 6–11, вопросы К-1, К-10, К-19–К-22.
3. Знак «*» у проёма — положение и размеры не замерены; реестр: листы 6–11, вопрос К-22.
4. Знак «*» у стояка — положение принято, не замерено (Ст К1-2*, Ст В1-2*); сверить на объекте до разметки. Реестр: листы 6–11, вопросы К-1, К-15, Кф-1.
5. За отметку ±0,000 принят чистый пол, не существующий (блок отметок). Н пот. — высота от чистого пола до плиты перекрытия; Н пот. со знаком «*» принятая высота, не замер (вопрос К-24).
6. Толщины стен: наружные 250 мм, перегородки 120 мм — приняты, не замерены (вопрос К-21); отличающиеся толщины и уступы — размерами на плане.
7. Несущие стены не определены: до технического заключения все стены считать несущими; проёмы и штробы в них не выполнять.
8. Дверные проёмы показаны без заполнения (двери — лист 22); высота дверных проёмов 2100 мм; низ окон (подоконник) 800, 900 мм от чистого пола, высота окон 1600, 1700 мм.
9. Диагонали — контрольные размеры; «*» — расчёт по принятому контуру, при обмере заменить замеренным; расхождение более 5 мм подписать на плане как перекос.
10. Размеры проверить на месте до начала работ; расхождение контрольных промеров ≤ 2 %.
11. Помещения, отмеченные *, в общую площадь квартиры не входят.
12. Размеры короче 1 мм на листе цепочкой не показаны (две выносные линии на таком расстоянии сливаются): пом. 5, стена А — 50 мм от угла до проёма.

1000 мм · печать 1:1

Изм.	Кол.уч	Лист	№ док.	Подп.	Дата
Разраб.		Кырлан А.С.			21.10.26
Пров.					
ГИП		Кырлан А.С.			21.10.26
Н. контр.					
Утв.					

ГД-2026-004-АИ

Четырёхкомнатная квартира

Общая площадь 102,67* м² · * размеры со скана, не замерены (реестр — л. 6–11, ИЗ-8, К-20, К-21)

Дизайн-проект интерьера четырёхкомнатной квартиры

Стадия	Лист	Листов
РП	20	124

Обмерный план

М 1:100

Кырлан Александр Сергеевич

выпуск 05.10.2026 № 7e7a2cd217 · стр. 23 из 168

План демонтажа и монтажа перегородок

Перепланировка не выполняется · существующие стены сохраняются · размеры в мм

ПРЕДВАРИТЕЛЬНО · не для производства работ · открыто пунктов: 30 (реестр — л. 6–11)

Условные обозначения

- существующие стены — сохраняются; несущие не определены — считать несущими
- демонтируемые конструкции — на плане нет
- возводимые перегородки — на плане нет
- проём существующий, без заполнения (откосы)
- (1) номер помещения, площадь м²
- * «*» — принято, не замерено и не подтверждено

Примечания

1. Перепланировка не выполняется: несущие и ненесущие стены, перегородки и плиты перекрытия не демонтируются, новые стены не возводятся; существующие стены и перегородки сохраняются.
2. Демонтаж существующих покрытий пола, стен и потолка, дверных блоков и сантехприборов (если есть) — до основания; объёмы демонтажа — для справки, по факту на объекте.
3. За отметку ±0,000 принят чистый пол, не существующий (блок отметок). Размеры — в мм по чистовой поверхности стен до отделки.
4. Размеры проверить на месте до начала работ: расхождение с обмером — не более 2 % (иначе — к архитектору).
5. Несущие стены не определены: до технического заключения все стены считать несущими — проёмы, ниши и штробы в них не выполнять.

Отметки по высоте

±0,000	чистый пол пом. 1, 3–9, 11, 12; отсчёт высот	**−0,170***	верх плиты — расчёт, не замер (задание на обмер)
−0,015	чистый пол пом. 2, 10, ниже на 15 мм	**сущ. пол**	снимается до плиты; не замерен (задание на обмер)
−0,030	чистый пол пом. 13, ниже на 30 мм		

Допущения и предложения на листе. Знак «*» принято (замерить). Знак «**» предложено (согласовать). См. лист открытых вопросов (листы 6–11).

1000 мм · печать 1:1

Изм.	Кол.уч	Лист	№ док.	Подп.	Дата
Разраб.		Кырлан А.С.			21.10.26
Пров.					
ГИП		Кырлан А.С.			21.10.26
Н. контр.					
Утв.					

ГД-2026-004-АИ

Четырёхкомнатная квартира

Общая площадь 102,67* м² · * размеры со скана, не замерены (реестр — л. 6–11, ИЗ-8, К-20, К-21)

Дизайн-проект интерьера четырёхкомнатной квартиры

Стадия	Лист	Листов
РП	21	124

План демонтажа и монтажа перегородок

М 1:50

Кырлан Александр Сергеевич

выпуск 05.10.2026 № 7e7a2cd217 · стр. 24 из 168

План дверей и ведомость заполнения проёмов

Проёмы, марки заполнения, привязки · размеры в мм

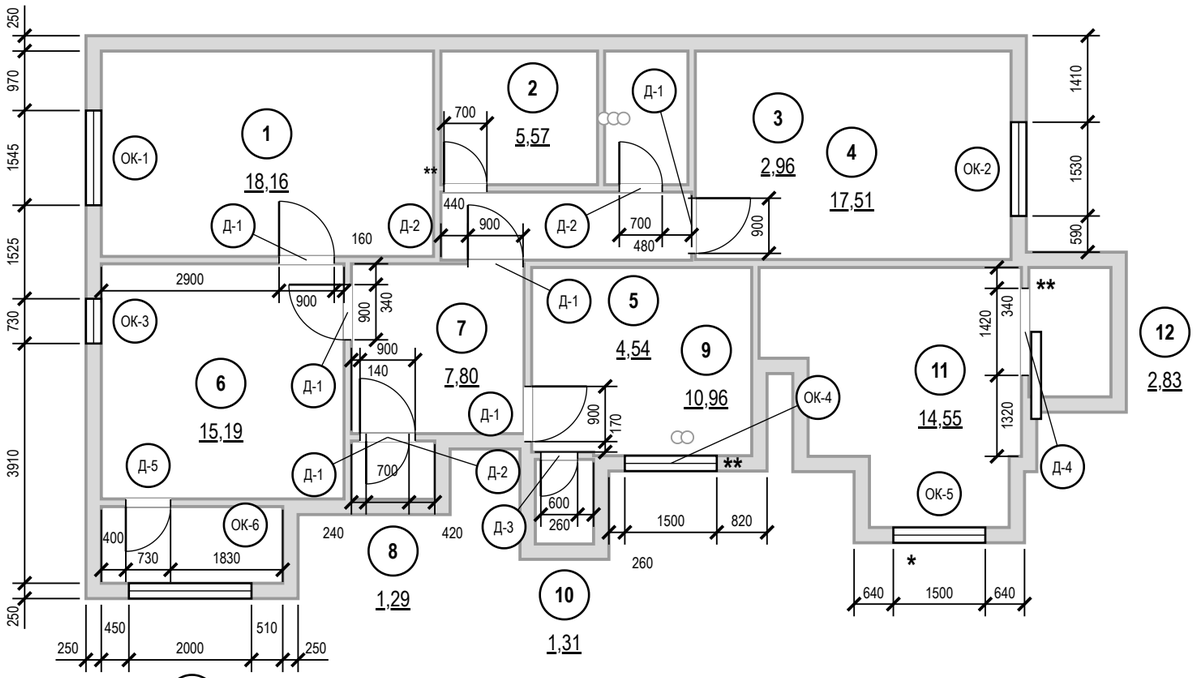

Ведомость заполнения проёмов

Марка	Наименование, обозначение	Проём ш×в, мм	Кол.	Откр.	Отделка полотна	Фурнитура	Прим.
Д-1	Блок дверной внутренний, ГОСТ 475-2016	900×2100	6	П, П, П, Л, П, П		петли, ручка с защёлкой	б/п
Д-2	Блок дверной внутренний, ГОСТ 475-2016	700×2100	3	П, П, Л		петли, ручка с защёлкой, фиксатор WC	** пом. 2; порог 15
Д-3	Блок дверной внутренний, ГОСТ 475-2016	600×2100	1	Л		петли, ручка с защёлкой, фиксатор WC	порог 15
Д-4	Дверь раздвижная, ГОСТ 475-2016	1420×2100	1			раздвижная система, ручки-купе	** пом. 12; б/п
Д-5	Блок дверной внутренний, ГОСТ 475-2016	730×2100	1	Л		петли, ручка с защёлкой	порог 30
ОК-1	Блок оконный, ГОСТ 23166-2021	1545×1600	1				низ 800
ОК-2	Блок оконный, ГОСТ 23166-2021	1530×1600	1				низ 800
ОК-3	Блок оконный, ГОСТ 23166-2021	730×1600	1				низ 800
ОК-4	Блок оконный, ГОСТ 23166-2021	1500×1600	1				** пом. 9; низ 800
ОК-5	Блок оконный, ГОСТ 23166-2021	1500×1600	1				* пом. 11; низ 900
ОК-6	Блок оконный, ГОСТ 23166-2021	2000×1700	1				низ 900

Условные обозначения

- стены (подложка обмера)
- дверь распашная, дуга открывания
- дверь раздвижная
- оконный блок
- (Д) — марка типа (Д-N, ОК-N)
- (1) — номер помещения, площадь м²
- * — «*» — принято, не замерено и не подтверждено
- ** — «**» — предложение проектировщика, заказчиком не утверждено

Примечания

1. Размеры проёмов и привязки — в миллиметрах от чистых граней стен до отделки; привязка — от угла того помещения, со стороны которого стоит размер. Размер в ведомости — ширина × высота проёма от чистого пола 0,000.
2. Марки в кружках — типы заполнения проёмов (ГОСТ 21.501-2018, п. 5.3.2); одна марка — один типоразмер; количество сверено с планом.
3. Открывание: Л — петли слева, П — справа, если смотреть со стороны, куда открывается полотно (на себя).
4. Дверные блоки обычного монтажа (Д-1…Д-5) заказывать после чистовой стяжки и штукатурки, проёмы перемерить; монтажный зазор коробки 10–15 мм на сторону, откос от угла помещения до коробки — не менее 50 мм.
5. Размеры проёмов и привязки сняты со скана плана заказчика и на объекте не замерены (обмерный план — лист 20).
6. Знак «*» у проёма — допущение: положение и размеры проёма не замерены (окно пом. 11, стена В); размер напечатан как принятый; в ведомости — знак «*» в графе «Прим.». Реестр: листы 6–11, вопрос К-22.
7. Экспликация помещений — лист 20; в марках помещений — номер и площадь, м².
8. Привязка проёма к углу помещения меньше 1 мм на листе, размер на плане не показан: Д-2 — 50 мм; Д-1 — 100 мм; Д-3 — 90 мм.

Допущения и предложения на листе

Основа листа: размеры сняты с размерных цепочек растрового скана плана заказчика, на объекте не замерены; ступени наружного контура приведены к граням помещений модели (ИЗ-8, К-20, К-21); высота потолка 2700 мм принята, источника нет (К-24); тип дома и перекрытие (монолит, плита 220 мм) приняты, источника нет (К-3); толщины стен приняты (250 и 120 мм), источника нет (К-21); мощность 15 кВт принята, технических условий нет (К-25).

Знак «*» — принято, не замерено и не подтверждено (замерить на объекте): К-1, К-15: Ст К1-2, Ст В1-2; К-22: окно пом. 11 (стена В).

Знак «**» — предложение проектировщика, заказчиком не утверждено (согласовать с заказчиком): ИЗ-1, К-1: окно пом. 9 (стена В); ИЗ-6: дверь пом. 12 (стена Г); ИЗ-8: дверь пом. 2 (стена В) — смещение 100 → 110 мм (откос до угла был 40 мм при норме от 50 мм).

См. лист открытых вопросов (лист 6, записи К-1, К-3; лист 7, записи К-15, К-20–К-22, К-24, К-25; лист 9, записи ИЗ-1, ИЗ-6; лист 10, запись ИЗ-8).

1000 мм · печать 1:1

Изм.	Кол.уч	Лист	№ док.	Подп.	Дата
Разраб.		Кырлан А.С.			21.10.26
Пров.					
ГИП		Кырлан А.С.			21.10.26
Н. контр.					
Утв.					

ГД-2026-004-АИ

Четырёхкомнатная квартира

Общая площадь 102,67* м² · * размеры со скана, не замерены (реестр — л. 6–11, ИЗ-8, К-20, К-21)

Дизайн-проект интерьера четырёхкомнатной квартиры

Стадия	Лист	Листов
РП	22	124

План дверей и ведомость заполнения проёмов

М 1:100

Кырлан Александр Сергеевич

выпуск 05.10.2026 № 7e7a2cd217 · стр. 25 из 168

02

Планировочное решение

Кырлан Александр Сергеевич

выпуск 05.10.2026 № 7e7a2cd217 · стр. 26 из 168

Концепция интерьера

Современный (контемпорари) · схема аналоговая · 60/30/10 · материалы, образы и зонирование

Идея

Квартира для семьи с двумя детьми. Из трёх вариантов планировки принят тот, где обеденная группа стоит в зале: у кухни два дверных проёма — из зала и из прихожей, — они съедают правую половину её стен, поэтому кухня остаётся рабочей (однорядный фронт и остров для завтраков), а зал 18,2 м² получает столовую на шесть персон. Стиль современный (контемпорари): актуальность, комфорт, мягкая геометрия, контраст фактур, открытость, уверенность. 60 % — тёплый белый Paper F497 и песочный Castle J484, 30 % — грейж Claystone V486 в фасадах встроенного хранения и текстиле, 10 % — коричнево-лиловый Silhouette L481 из палитры стиля: ТВ-стена зала, изголовья детских, фасад кухонного острова. По практике тёплая аналоговая гамма ровнее держит цвет в квартире с окнами на разные стороны. Цветовая схема — аналоговая, пропорция 60/30/10: база на стенах и потолках, вторичный цвет — в текстиле и мягкой мебели, акцент — точечно.

Мудборд: материалы и фактуры

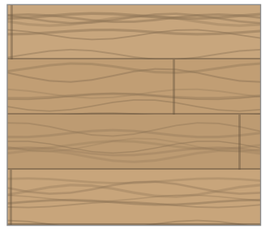

Дуб натуральный брашированный, масло-воск
пол

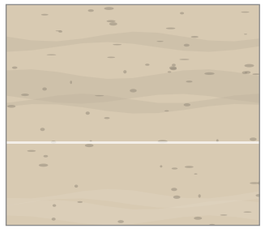

Керамогранит матовый R10
пол

Paper · Tikkurila F497
стены, потолок, плинтус

Castle · Tikkurila J484
стены, плинтус

Silhouette · Tikkurila L481
акцент (стена А)

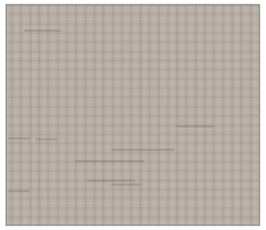

Лён, Tikkurila V486
Портьеры-волна, Рулонная штора кассетная

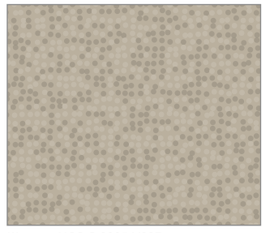

Шерсть, NCS S 3005-Y20R
Ковёр мягкой группы, Ковёр прихожей

Бархат, Tikkurila L481
Подушки декоративные на диван

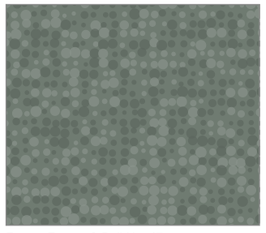

Букле, Farrow & Ball No. 47
Подушка декоративная

Палитра 60/30/10

60 %	30 %	10 %

60 % база — Tikkurila F497 Paper, LRV 88; Tikkurila J484 Castle, LRV 55

30 % вторичный — Tikkurila V486 Claystone, LRV 44

10 % акцент — Tikkurila L481 Silhouette, LRV 18

Функциональное зонирование (М 1:200)

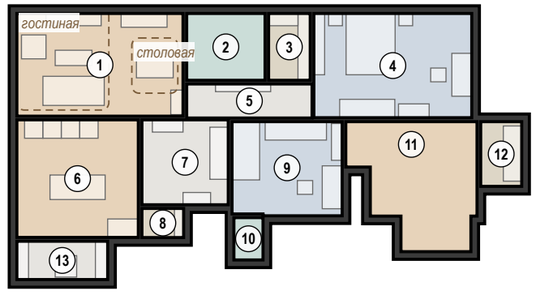

- дневная зона: гостиная, кухня, столовая
- ночная зона: спальни
- мокрая зона: санузлы
- хранение: гардеробная, кладовая
- вход и коммуникации
- функциональная зона в помещении
- (1) номер помещения (лист 24)

Образы помещений

1. Зал 18,16 м²
стены Tikkurila F497; акцент L481 на стене А

11. Гостиная 14,55 м²
стены Tikkurila F497; акцент L481 на стене А

6. Кухня 15,19 м²
стены Tikkurila F497

4. Детская 1 17,51 м²
стены Tikkurila F497

9. Детская 2 10,96 м²
стены Tikkurila F497

7. Прихожая-коридор 7,80 м²
стены Tikkurila J484

5. Коридор 4,54 м²
стены Tikkurila J484

8. Гардеробная 2 1,29 м²
стены Tikkurila F497

12. Гардеробная 1 2,83 м²
стены Tikkurila F497

2. Ванная комната 5,57 м²
стены #F1F1EC

10. Санузел 1,31 м²
стены #F1F1EC

3. Тёмная комната 2,96 м²
стены Tikkurila F497

13. Балкон 1 3,70 м²
стены Tikkurila F497

Материалы и отделка

Дуб натуральный брашированный, масло-воск
14/4 мм
пол — пом. 1, 3, 4, 6, 8, 9, 11, 12

Керамогранит матовый R10
тон J484; 600×600
пол — пом. 2, 10

Керамогранит матовый
тон F497; 600×600
стены, фартук — пом. 2, 6, 10

Керамогранит матовый R10
тон V486; 600×600
пол — пом. 5, 7

Керамогранит матовый R11
тон V486; 600×600
пол — пом. 13

Плинтус из керамогранита пола
подрезка 80 мм, верхняя кромка с запилом 45°
плинтус — пом. 13

Tikkurila F497 Paper, LRV 88
Tikkurila Optiva 5 Matt, матовая
стены, потолок, плинтус — пом. 1, 2, 3, 4, 5, 6, 7, 8, 9, 10, 11, 12, 13

Tikkurila J484 Castle, LRV 55
Tikkurila Optiva 20 Semimatt
стены, плинтус — пом. 5, 7

Tikkurila L481 Silhouette, LRV 18
акцентная стена
акцент (стена А) — пом. 1, 11

Текстиль и металл

Лён, Tikkurila V486
Портьеры-волна, Рулонная штора кассетная

Вуаль, Tikkurila F497
Тюль-вуаль

Шерсть, NCS S 3005-Y20R
Ковёр мягкой группы, Ковёр прихожей

Лён, Tikkurila H487
Подушки декоративные на диван, Римская штора блэкаут: окно закрывает она

Бархат, Tikkurila L481
Подушки декоративные на диван

Шерсть, Tikkurila L481
Плед на диван

Лён, Tikkurila J484
Раннер на обеденный стол, Рулонная штора кассетная

Лён, Tikkurila V484
Портьеры стационарные

Шерсть, Tikkurila H487
Ковёр у кровати

Бархат, NCS S 5010-B10G
Подушка декоративная

Чего избегаем

1) Смешение трёх и более металлов в одной комнате
2) Мебель из каталога всё сразу одной коллекции — теряется слоистость
3) Тренды без базы: весь интерьер на букле и арках к 2027 устареет
4) Глянцевый натяжной потолок и хромированные хай-тек детали 2000-х
5) Перегрузка акцентами разного цвета (синий + зелёный + терракота в одной комнате)
6) Холодный свет 4000 К в жилых зонах

Допущения и предложения на листе

Основа листа: размеры сняты с размерных цепочек растрового скана плана заказчика, на объекте не замерены; ступени наружного контура приведены к граням помещений модели (ИЗ-8, К-20, К-21); высота потолка 2700 мм принята, источника нет (К-24); тип дома и перекрытие (монолит, плита 220 мм) приняты, источника нет (К-3); толщины стен приняты (250 и 120 мм), источника нет (К-21); мощность 15 кВт принята, технических условий нет (К-25).

Изменения по листу без подписи: ИЗ-7.

См. лист открытых вопросов (лист 6, запись К-3; лист 7, записи К-20, К-21, К-24, К-25; лист 9, запись ИЗ-7; лист 10, запись ИЗ-8).

Примечания

1. Коды цвета — по веерам производителей (колерная карта, лист 58); перед закупкой краски — выкрас на стене объекта под дневным светом и лампами проекта.
2. Материалы — по ведомости отделки (лист 55); мебель, текстиль и декор — по спецификации (лист 25). Образцы доски, керамогранита и тканей утвердить до заказа.
3. Фактуры на листе условные, цвет передан по HEX-значениям производителей: при печати возможны отклонения, решение — только по физическому образцу.

Изм.	Кол.уч	Лист	№ док.	Подп.	Дата
Разраб.		Кырлан А.С.			21.10.26
Пров.					
ГИП		Кырлан А.С.			21.10.26
Н. контр.					
Утв.					

ГД-2026-004-АИ

Четырёхкомнатная квартира

Общая площадь 102,67* м² · * размеры со скана, не замерены (реестр — л. 6–11, ИЗ-8, К-20, К-21)

Дизайн-проект интерьера четырёхкомнатной квартиры

Стадия	Лист	Листов
РП	23	124

Концепция интерьера
М б/м

Кырлан Александр Сергеевич

выпуск 05.10.2026 № 7e7a2cd217 · стр. 27 из 168

План расстановки мебели

Мебель и оборудование · размеры в мм от чистовых стен · марки — по ведомости

ПРЕДВАРИТЕЛЬНО · не для производства работ · открыто пунктов: 30 (реестр — л. 6–11)

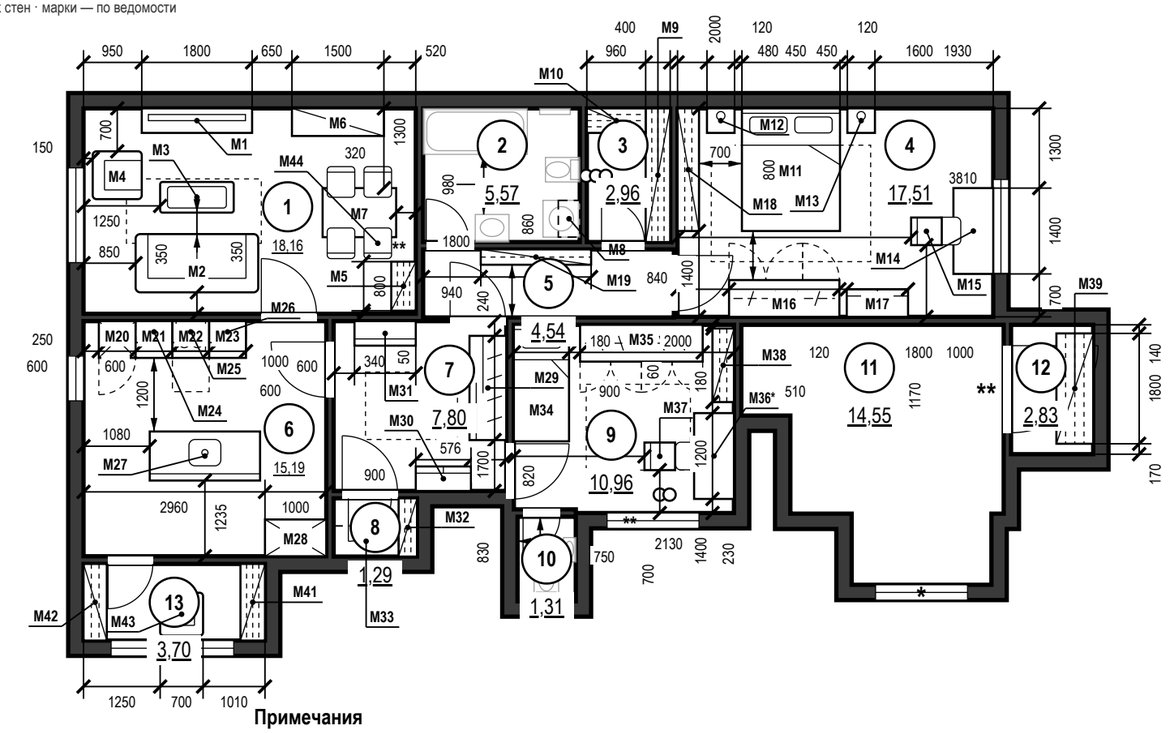

Примечания

1. Размеры — в мм от чистовых поверхностей стен, привязки — от стен и углов помещения, проходы и зазоры — стрелками; розетки и выводы под мебель лист 29, выключатели — лист 31, сантехприборы — лист 40.
2. Общие указания к расстановке (чистовой слой, контрольный обмер, зазоры встроенной мебели, замена покупной) — примечания к спецификации, лист 25.
3. Отступ от стены, на плане не образмерен: М43 — 80 мм.
4. Стулья обеденной группы (М44 — 4 шт.) показаны в рабочем положении, задвинутыми под столешницу на 150 мм.

Экспликация помещений

лист 20 · на плане — номера в марках

Ведомость мебели и оборудования

43 позиц. (46 шт.) — не помещается на листе:
полностью на листе 25 «Спецификация мебели и оборудования»
марка, наименование, Ш×Г×В, материал, модель,
допуск замены. Марки на плане — по ней.

Условные обозначения

- мебель и оборудование — габарит в масштабе
- навесные шкафы (низ выше 0,9 м) — невидимый контур
- ковёр
- зона открывания дверец шкафов и техники
- К1 — марка предмета по ведомости мебели
- привязка от чистовой стены, мм
- ширина прохода, зазор, мм
- сантехприборы — подложка (лист ВК)
- существующие стены (сечение)
- * — «*» — принято, не замерено и не подтверждено
- ** — «**» — предложение проектировщика, заказчиком не утверждено
- стояк: К1 — канализация, В1 — ХВС, Т3 — ГВС
- 1 — номер помещения, площадь м²

Допущения и предложения на листе

Основа листа: размеры сняты с размерных цепочек растрового скана плана заказчика, на объекте не замерены; ступени наружного контура приведены к граням помещений модели (ИЗ-8, К-20, К-21); высота потолка 2700 мм принята, источника нет (К-24); тип дома и перекрытие (монолит, плита 220 мм) приняты, источника нет (К-3); толщины стен приняты (250 и 120 мм), источника нет (К-21); мощность 15 кВт принята, технических условий нет (К-25).
Знак «*» — принято, не замерено и не подтверждено (замерить на объекте): ИЗ-1, К-13: М36 — положение и размеры стола утверждены автором (ИЗ-1); боковой свет от окна справа принят допустимым, рабочая рука того, кто сидит за столом, не известна (К-13); К-1, К-15: Ст К1-2, Ст В1-2; К-22: окно пом. 11 (стена В).
Знак «**» — предложение проектировщика, заказчиком не утверждено (согласовать с заказчиком): ИЗ-1, К-1: окно пом. 9 (стена В); ИЗ-6: дверь пом. 12 (стена Г); ИЗ-8: дверь пом. 2 (стена В) — смещение 100 → 110 мм (откос до угла был 40 мм при норме от 50 мм).
Открытые вопросы и конфликты по листу: К-4, К-13, К-20.
Изменения по листу без подписи: ИЗ-11.
См. лист открытых вопросов (лист 6, записи К-1, К-3, К-4, К-13; лист 7, записи К-15, К-20–К-22, К-24, К-25; лист 9, записи ИЗ-1, ИЗ-6; лист 10, записи ИЗ-8, ИЗ-11).

1000 мм · печать 1:1

Изм.	Кол.уч	Лист	№ док.	Подп.	Дата
Разраб.		Кырлан А.С.			21.10.26
Пров.					
ГИП		Кырлан А.С.			21.10.26
Н. контр.					
Утв.					

ГД-2026-004-АИ

Четырёхкомнатная квартира

Общая площадь 102,67* м² · * размеры со скана, не замерены (реестр — л. 6–11, ИЗ-8, К-20, К-21)

Дизайн-проект интерьера четырёхкомнатной квартиры

Стадия	Лист	Листов
РП	24	124

План расстановки мебели

М 1:100

Кырлан Александр Сергеевич

выпуск 05.10.2026 № 7e7a2cd217 · стр. 28 из 168

Спецификация мебели и оборудования

ПРЕДВАРИТЕЛЬНО · не для производства работ · открыто пунктов: 30 (реестр — л. 6–11)

Форма 1 ГОСТ 21.110-2013 · позиции мебели — по плану расстановки

Поз.	Наименование и техническая характеристика	Тип, марка, обозначение документа, опросного листа	Код продукции	Поставщик	Ед. измерения	Кол.	Масса 1 ед., кг	Примечание
	Мебель встроенная и корпусная (изготовление по чертежам мебельщика)							
М9	Стеллаж хозяйственный, 6 полок; дерево — дуб натуральный; Ш×Г×В 2180×400×2400 мм			изготовление на заказ	шт.	1		пом. 3; крепление к стене
М10	Стеллаж хозяйственный, 6 полок; дерево — дуб натуральный; Ш×Г×В 960×400×2400 мм			изготовление на заказ	шт.	1		пом. 3; крепление к стене
М16	Шкаф распашной, 3 секции; дерево — дуб натуральный; Ш×Г×В 1800×600×2400 мм			изготовление на заказ	шт.	1		пом. 4; крепление к стене
М19	Шкаф хозяйственный неглубокий; дерево — дуб натуральный; Ш×Г×В 1800×250×2400 мм			изготовление на заказ	шт.	1		пом. 5; крепление к стене
М20	Пенал кухонный с встроенным холодильником; дерево — дуб натуральный, металл — чёрный матовый; Ш×Г×В 600×600×2300 мм			изготовление на заказ	шт.	1		пом. 6; крепление к стене
М21	Модуль нижний, ящики; металл — чёрный матовый; Ш×Г×В 600×600×900 мм			изготовление на заказ	шт.	1		пом. 6
М22	Модуль нижний: варочная панель и духовой шкаф; металл — чёрный матовый; Ш×Г×В 600×600×900 мм			изготовление на заказ	шт.	1		пом. 6
М23	Модуль нижний, ящики и бутылочница; металл — чёрный матовый; Ш×Г×В 600×600×900 мм			изготовление на заказ	шт.	1		пом. 6
М24	Модуль навесной, 2 секции; металл — чёрный матовый; Ш×Г×В 600×350×720 мм			изготовление на заказ	шт.	1		пом. 6
М25	Вытяжка встраиваемая в шкаф; металл — чёрный матовый; Ш×Г×В 600×350×600 мм			изготовление на заказ	шт.	1		пом. 6
М26	Модуль навесной, 2 секции; металл — чёрный матовый; Ш×Г×В 600×350×720 мм			изготовление на заказ	шт.	1		пом. 6
М27	Остров кухонный с мойкой и посудомоечной машиной; дерево — дуб натуральный, металл — чёрный матовый; Ш×Г×В 1800×800×900 мм			изготовление на заказ	шт.	1		пом. 6
М28	Пенал-кладовая кухонная; дерево — дуб натуральный, металл — чёрный матовый; Ш×Г×В 1000×600×2300 мм			изготовление на заказ	шт.	1		пом. 6; крепление к стене
М29	Шкаф-купе, 3 двери; дерево — дуб натуральный, металл — чёрный матовый; Ш×Г×В 1700×600×2400 мм			изготовление на заказ	шт.	1		пом. 7; крепление к стене
М32	Система хранения: штанга, полки, ящики; дерево — дуб натуральный; Ш×Г×В 950×300×2400 мм			изготовление на заказ	шт.	1		пом. 8; крепление к стене
М33	Антресоль над зоной открывания двери; дерево — дуб натуральный; Ш×Г×В 1060×500×300 мм			изготовление на заказ	шт.	1		пом. 8; крепление к стене
М35	Шкаф распашной, 4 секции; дерево — дуб натуральный; Ш×Г×В 2000×600×2400 мм			изготовление на заказ	шт.	1		пом. 9; крепление к стене
М39	Система хранения торцевая: штанги, полки; дерево — дуб натуральный; Ш×Г×В 1800×600×2400 мм			изготовление на заказ	шт.	1		пом. 12; крепление к стене
М41	Шкаф хозяйственный балконный; дерево — дуб натуральный; Ш×Г×В 1250×400×2000 мм			изготовление на заказ	шт.	1		пом. 13; крепление к стене
М42	Шкаф хозяйственный балконный; дерево — дуб натуральный; Ш×Г×В 1250×380×2000 мм			изготовление на заказ	шт.	1		пом. 13; крепление к стене
	Мебель покупная							
М1	ТВ-тумба с экраном 55" дерево — дуб натуральный, металл — латунь; Ш×Г×В 1800×400×500 мм	тумба ТВ подвесная, 3 ящика		аналог по характеристикам	шт.	1		пом. 1; допуск замены Ш 1700–1900, Г ≤ 450
М2	Диван прямой трёхместный; обивка букле; Ш×Г×В 2000×950×800 мм	диван прямой, глубокая посадка, съёмные чехлы		аналог по характеристикам	шт.	1		пом. 1; допуск замены Ш 1900–2100, Г ≤ 1000
М3	Стол журнальный; дерево — дуб натуральный; Ш×Г×В 1200×500×400 мм	стол журнальный прямоугольный		аналог по характеристикам	шт.	1		пом. 1; допуск замены Ш 1100–1300
М4	Кресло у окна; обивка — ткань, цвет Tikkurila V486; Ш×Г×В 780×800×780 мм	кресло мягкое на деревянных ножках		аналог по характеристикам	шт.	1		пом. 1; допуск замены Ш 750–850, В ≤ 790 (не выше подоконника)
М5	Стеллаж-витрина; дерево — дуб натуральный, металл — латунь; Ш×Г×В 800×400×2100 мм	стеллаж открытый, 5 полок		аналог по характеристикам	шт.	1		пом. 1; крепление к стене; допуск замены Ш 750–850

Примечания

1. Позиции мебели совпадают с марками на плане расстановки (лист 24); размеры Ш×Г×В — Ш вдоль стены, Г от стены.
2. Размеры и привязки плана расстановки — в мм от чистовых поверхностей стен: слой штукатурки 20 мм по блоку и 5 мм шпаклёвки по ГКЛ учтён; привязки — от стен и углов помещения, а не от другой мебели.
3. План расстановки не является документацией для изготовления мебели. Встроенная и корпусная мебель изготавливается по чертежам мебельщика после контрольного обмера (после штукатурки); «стена в стену» — с зазором 10 мм с каждой стороны или с компенсаторами; графы «Тип, марка» и «Код продукции» для неё не заполняются (ГОСТ 21.110-2013).
4. Покупные изделия — аналог по характеристикам: заменять только на изделия не больше указанного габарита и того же материала и цвета.
5. Материал и цвет, не указанные в данных изделия, приняты по концепции (лист 23): тон дерева — по полу, обивка — по вторичному цвету палитры; образцы согласовать до заказа.
6. Масса 1 ед. для изделий до 25 кг не указывается. Техника — по монтажным схемам изготовителя; выводы — по листам ЭОМ и ВК.

Допущения и предложения на листе

Основа листа: размеры сняты с размерных цепочек растрового скана плана заказчика, на объекте не замерены; ступени наружного контура приведены к граням помещений модели (ИЗ-8, К-20, К-21); высота потолка 2700 мм принята, источника нет (К-24); тип дома и перекрытие (монолит, плита 220 мм) приняты, источника нет (К-3); толщины стен приняты (250 и 120 мм), источника нет (К-21); мощность 15 кВт принята, технических условий нет (К-25).
См. лист открытых вопросов (лист 6, запись К-3; лист 7, записи К-20, К-21, К-24, К-25; лист 10, запись ИЗ-8).

Изм.	Кол.уч	Лист	№ док.	Подп.	Дата
Разраб.		Кырлан А.С.			21.10.26
Пров.					
ГИП		Кырлан А.С.			21.10.26
Н. контр.					
Утв.					

ГД-2026-004-АИ

Четырёхкомнатная квартира

Общая площадь 102,67* м² · * размеры со скана, не замерены (реестр — л. 6–11, ИЗ-8, К-20, К-21)

Дизайн-проект интерьера четырёхкомнатной квартиры

Стадия	Лист	Листов
РП	25	124

Спецификация мебели и оборудования

М б/м

Кырлан Александр Сергеевич

выпуск 05.10.2026 № 7e7a2cd217 · стр. 29 из 168

Спецификация мебели и оборудования (продолжение)

Форма 1 ГОСТ 21.110-2013 · позиции мебели — по плану расстановки

ПРЕДВАРИТЕЛЬНО · не для производства работ · открыто пунктов: 30 (реестр — л. 6–11)

Поз.	Наименование и техническая характеристика	Тип, марка, обозначение документа, опросного листа	Код продукции	Поставщик	Ед. измерения	Кол.	Масса 1 ед., кг	Примечание
М6	Буфет обеденной зоны; дерево — дуб натуральный, металл — латунь; Ш×Г×В 1500×450×900 мм	буфет 3-дверный		аналог по характеристикам	шт.	1		пом. 1; крепление к стене; допуск замены Ш 1400–1600, Г ≤ 470
М7	Стол обеденный на 6 персон; дерево — дуб натуральный; Ш×Г×В 1200×800×750 мм	стол обеденный прямоугольный, раскладной до 1800		аналог по характеристикам	шт.	1		пом. 1; допуск замены Ш 1200–1400 в сложенном виде, Г 800–900
М44	Стул обеденный к столу М7; обивка — ткань, цвет Tikkurila V486; каркас — дуб натуральный; Ш×Г×В 450×500×820 мм			аналог по характеристикам	шт.	4		пом. 1; замена ≤ габарита
М8	Шкаф навесной над стиральной машиной; дерево — дуб натуральный, металл — хром; Ш×Г×В 600×350×700 мм			аналог по характеристикам	шт.	1		пом. 2; крепление к стене; замена ≤ габарита
М11	Кровать 1600×2000; мягкое изголовье, обивка — ткань, цвет Tikkurila V486; Ш×Г×В 1600×2000×450 мм	кровать с мягким изголовьем		аналог по характеристикам	шт.	1		пом. 4; допуск замены Ш 1600, Д 2000–2050
М12, М13	Тумба прикроватная; дерево — дуб натуральный; Ш×Г×В 450×400×550 мм	тумба прикроватная, 2 ящика		аналог по характеристикам	шт.	2		пом. 4; допуск замены Ш 400–500
М14	Стол письменный у окна; дерево — дуб натуральный, металл — чёрный матовый; Ш×Г×В 1400×650×750 мм	стол письменный с тумбой		аналог по характеристикам	шт.	1		пом. 4; допуск замены Ш 1300–1500, Г 600–700
М15, М37	Кресло рабочее; металл — чёрный матовый; Ш×Г×В 450×500×950 мм	кресло рабочее на роликах		аналог по характеристикам	шт.	2		пом. 4, 9; допуск замены Ш 480–560
М17	Комод, 4 ящика; дерево — дуб натуральный; Ш×Г×В 1000×450×850 мм	комод 4 ящика		аналог по характеристикам	шт.	1		пом. 4; крепление к стене; допуск замены Ш 950–1100
М18	Стеллаж книжный открытый; дерево — дуб натуральный; Ш×Г×В 2000×350×2100 мм			аналог по характеристикам	шт.	1		пом. 4; крепление к стене; замена ≤ габарита
М30	Банкетка-обувница с мягким сиденьем; дерево — дуб натуральный; Ш×Г×В 900×400×450 мм	банкетка-обувница		аналог по характеристикам	шт.	1		пом. 7; допуск замены Ш 800–950
М31	Консоль прихожей, 3 ящика; дерево — дуб натуральный, металл — чёрный матовый; Ш×Г×В 1000×400×850 мм	консоль-комод		аналог по характеристикам	шт.	1		пом. 7; крепление к стене; допуск замены Ш 950–1100
М34	Кровать 900×1900; мягкое изголовье, обивка — ткань, цвет Tikkurila V486; Ш×Г×В 900×1900×450 мм	кровать односпальная с мягким изголовьем		аналог по характеристикам	шт.	1		пом. 9; допуск замены Ш 900, Д 1900–1950
М36*	Стол письменный у стены Б, рядом с окном стены В: свет боковой; дерево — дуб натуральный, металл — чёрный матовый; Ш×Г×В 1400×650×750 мм	стол письменный с тумбой		аналог по характеристикам	шт.	1		пом. 9; допуск замены Ш 1300–1500, Г 600–700
М38	Стеллаж книжный; дерево — дуб натуральный; Ш×Г×В 1200×350×2100 мм			аналог по характеристикам	шт.	1		пом. 9; крепление к стене; замена ≤ габарита
М43	Кресло балконное; металл — чёрный матовый; Ш×Г×В 700×700×780 мм	кресло на металлическом каркасе		аналог по характеристикам	шт.	1		пом. 13; допуск замены Ш 650–750, В ≤ 850 (не выше подоконника)
	Техника встраиваемая и бытовая, светильники под розетки							
	Стиральная машина встраиваемая, у М8			аналог по характеристикам	шт.	1		пом. 2; по схеме изготовителя
	Холодильник встраиваемый, в модуле М20			аналог по характеристикам	шт.	1		пом. 6; по схеме изготовителя
	Духовой шкаф встраиваемый, в модуле М22			аналог по характеристикам	шт.	1		пом. 6; по схеме изготовителя
	Варочная панель встраиваемая, электрическая, в модуле М22			аналог по характеристикам	шт.	1		пом. 6; по схеме изготовителя
	Вытяжка встраиваемая, в модуле М25			аналог по характеристикам	шт.	1		пом. 6; по схеме изготовителя

Допущения и предложения на листе

Основа листа: размеры сняты с размерных цепочек растрового скана плана заказчика, на объекте не замерены; ступени наружного контура приведены к граням помещений модели (ИЗ-8, К-20, К-21); высота потолка 2700 мм принята, источника нет (К-24); тип дома и перекрытие (монолит, плита 220 мм) приняты, источника нет (К-3); толщины стен приняты (250 и 120 мм), источника нет (К-21); мощность 15 кВт принята, технических условий нет (К-25).

Знак «*» — принято, не замерено и не подтверждено (замерить на объекте): ИЗ-1, К-13: М36 — положение и размеры стола утверждены автором (ИЗ-1); боковой свет от окна справа принят допустимым, рабочая рука того, кто сидит за столом, не известна (К-13).

См. лист открытых вопросов (лист 6, записи К-3, К-13; лист 7, записи К-20, К-21, К-24, К-25; лист 9, запись ИЗ-1; лист 10, запись ИЗ-8).

Изм.	Кол.уч	Лист	№ док.	Подп.	Дата
Разраб.		Кырлан А.С.			21.10.26
Пров.					
ГИП		Кырлан А.С.			21.10.26
Н. контр.					
Утв.					

ГД-2026-004-АИ

Четырёхкомнатная квартира

Общая площадь 102,67* м² · * размеры со скана, не замерены (реестр — л. 6–11, ИЗ-8, К-20, К-21)

Дизайн-проект интерьера четырёхкомнатной квартиры	Стадия	Лист	Листов
	РП	26	124
Спецификация мебели и оборудования (продолжение) М б/м	**Кырлан Александр Сергеевич**		

выпуск 05.10.2026 № 7e7a2cd217 · стр. 30 из 168

Спецификация мебели и оборудования (продолжение)

Форма 1 ГОСТ 21.110-2013 · позиции мебели — по плану расстановки

Поз.	Наименование и техническая характеристика	Тип, марка, обозначение документа, опросного листа	Код продукции	Поставщик	Ед. измерения	Кол.	Масса 1 ед., кг	Примечание
	Посудомоечная машина встраиваемая, в модуле M27; ниша 600 мм			аналог по характеристикам	шт.	1		пом. 6; по схеме изготовителя
	Торшер, у поз. M2; абажур — ткань или опаловое стекло; лампа 2700 K			аналог по характеристикам	шт.	1		пом. 1; розетка Р3 (ЭОМ)
	Текстиль							
T1	Портьеры-волна, два полотна; лён 100 %; цвет Tikkurila V486; карниз 2150 мм, высота 2690 мм, сборка 2			аналог по характеристикам	шт.	2		пом. 1
T2	Тюль-вуаль, одно полотно; полиэстер 100 %; цвет Tikkurila F497; карниз 2150 мм, высота 2690 мм, сборка 2,5			аналог по характеристикам	шт.	1		пом. 1
T3	Ковёр мягкой группы; шерсть 100 %; цвет NCS S 3005-Y20R; 2200×1050 мм			аналог по характеристикам	шт.	1		пом. 1; с подложкой
T4	Подушки декоративные на диван; лён 100 %; цвет Tikkurila H487			аналог по характеристикам	шт.	3		пом. 1
T5	Подушки декоративные на диван, акцент; хлопковый бархат 100 %; цвет Tikkurila L481			аналог по характеристикам	шт.	2		пом. 1
T6	Плед на диван; шерсть мериноса 100 %; цвет Tikkurila L481			аналог по характеристикам	шт.	1		пом. 1
T7	Раннер на обеденный стол; лён 100 %; цвет Tikkurila J484			аналог по характеристикам	шт.	1		пом. 1
T8	Портьеры стационарные, два полотна; лён 55 %, хлопок 45 %; цвет Tikkurila V484; карниз 2140 мм, высота 2690 мм, сборка 2			аналог по характеристикам	шт.	2		пом. 4
T9	Римская штора блэкаут: окно закрывает она, стол M14 у окна не мешает; хлопок 100 %, подкладка полиэстер; цвет Tikkurila H487; карниз 1650 мм, высота 1900 мм			аналог по характеристикам	шт.	1		пом. 4
T10	Ковёр у кровати; шерсть 80 %, хлопок 20 %; цвет Tikkurila H487; 2600×1900 мм			аналог по характеристикам	шт.	1		пом. 4; с подложкой
T11	Подушки декоративные на кровать; лён 100 %; цвет Tikkurila H487			аналог по характеристикам	шт.	2		пом. 4
T12	Подушка декоративная, акцент; хлопковый бархат 100 %; цвет NCS S 5010-B10G			аналог по характеристикам	шт.	1		пом. 4
T13	Плед на кровать; хлопок 100 %; цвет NCS S 5010-B10G			аналог по характеристикам	шт.	1		пом. 4
T14	Рулонная штора кассетная, ткань димаут; полиэстер 100 %; цвет Tikkurila J484; карниз 890 мм, высота 1900 мм			аналог по характеристикам	шт.	1		пом. 6
T15	Ковёр прихожей, низкий ворс; шерсть 80 %, полиамид 20 %; цвет NCS S 3005-Y20R; 1500×1100 мм			аналог по характеристикам	шт.	1		пом. 7; с подложкой
T16**	Портьеры стационарные, два полотна, до подоконника: радиатор под окном открыт; лён 55 %, хлопок 45 %; цвет Tikkurila V484; карниз 1800 мм, высота 1930 мм, сборка 2			аналог по характеристикам	шт.	2		пом. 9
T17**	Римская штора блэкаут: закрывает проём целиком, радиатор под окном не задевает; хлопок 100 %, подкладка полиэстер; цвет Tikkurila H487; карниз 1620 мм, высота 1900 мм			аналог по характеристикам	шт.	1		пом. 9
T18	Ковёр игровой зоны; шерсть 100 %; цвет NCS S 3005-Y20R; 1700×1400 мм			аналог по характеристикам	шт.	1		пом. 9; с подложкой
T19	Подушки декоративные на кровать; лён 100 %; цвет Tikkurila H487			аналог по характеристикам	шт.	2		пом. 9
T20	Подушка декоративная, акцент; шерсть 60 %, полиэстер 40 %; цвет Farrow & Ball No. 47			аналог по характеристикам	шт.	1		пом. 9
T21	Плед на кровать; хлопок 100 %; цвет Farrow & Ball No. 47			аналог по характеристикам	шт.	1		пом. 9
T22	Рулонная штора кассетная, солнцезащитная; полиэстер 100 %; цвет Tikkurila V486; карниз 2140 мм, высота 1700 мм			аналог по характеристикам	шт.	1		пом. 13
T23	Плед на кресло M43; шерсть 100 %; цвет Tikkurila V484			аналог по характеристикам	шт.	1		пом. 13
	Декор							
ДК1	Картина над диваном: крупная абстракция, холст, тонкая рама; 1400×900 мм; низ на 1000 мм от пола			аналог по характеристикам	шт.	1	6	пом. 1; крепление: планка на дюбелях, 4 точки

Допущения и предложения на листе

Основа листа: размеры сняты с размерных цепочек растрового скана плана заказчика, на объекте не замерены; ступени наружного контура приведены к граням помещений модели (ИЗ-8, К-20, К-21); высота потолка 2700 мм принята, источника нет (К-24); тип дома и перекрытие (монолит, плита 220 мм) приняты, источника нет (К-3); толщины стен приняты (250 и 120 мм), источника нет (К-21); мощность 15 кВт принята, технических условий нет (К-25).

Знак «**» — предложение проектировщика, заказчиком не утверждено (согласовать с заказчиком): ИЗ-1: T16, T17.

См. лист открытых вопросов (лист 6, запись К-3; лист 7, записи К-20, К-21, К-24, К-25; лист 9, запись ИЗ-1; лист 10, запись ИЗ-8).

Изм.	Кол.уч	Лист	№ док.	Подп.	Дата
Разраб.		Кырлан А.С.			21.10.26
Пров.					
ГИП		Кырлан А.С.			21.10.26
Н. контр.					
Утв.					

ГД-2026-004-АИ

Четырёхкомнатная квартира

Общая площадь 102,67* м² · * размеры со скана, не замерены (реестр — л. 6–11, ИЗ-8, К-20, К-21)

Дизайн-проект интерьера четырёхкомнатной квартиры

Стадия	Лист	Листов
РП	27	124

Спецификация мебели и оборудования (продолжение)
М б/м

Кырлан Александр Сергеевич

выпуск 05.10.2026 № 7e7a2cd217 · стр. 31 из 168

Спецификация мебели и оборудования (продолжение)

Форма 1 ГОСТ 21.110-2013 · позиции мебели — по плану расстановки

Поз.	Наименование и техническая характеристика	Тип, марка, обозначение документа, опросного листа	Код продукции	Поставщик	Ед. измерения	Кол.	Масса 1 ед., кг	Примечание
ДК2	Зеркало над буфетом, рама шпон дуба; 1000×800 мм; низ на 1100 мм от пола			аналог по характеристикам	шт.	1	12	пом. 1; крепление: анкер химический, 4 точки
ДК3	Фикус лировидный в кашпо Ø400; 450×450 мм			аналог по характеристикам	шт.	1		пом. 1
ДК4	Зеркало над раковиной П3, влагостойкое; 600×800 мм; низ на 1100 мм от пола			аналог по характеристикам	шт.	1	5	пом. 2; крепление: зеркалодержатели, 4 точки
ДК5	Картина над изголовьем: графика, паспарту, рама; 1100×700 мм; низ на 1300 мм от пола			аналог по характеристикам	шт.	1	4	пом. 4; крепление: две петли на дюбелях
ДК6	Зеркало над комодом М17; 700×900 мм; низ на 1050 мм от пола			аналог по характеристикам	шт.	1	8	пом. 4; крепление: анкер химический, 4 точки
ДК7	Хлорофитум хохлатый в напольном кашпо Ø380; 420×420 мм			аналог по характеристикам	шт.	1		пом. 4
ДК8	Часы настенные Ø400; 400×400 мм; центр на 1550 мм от пола			аналог по характеристикам	шт.	1	2	пом. 6; крепление: дюбель с крюком, 1 точка
ДК9	Хлорофитум хохлатый на подоконнике (отм. +0,800); 300×200 мм; низ на 800 мм от пола			аналог по характеристикам	шт.	1		пом. 6
ДК10	Зеркало над консолью М31; 700×1000 мм; низ на 1050 мм от пола			аналог по характеристикам	шт.	1	9	пом. 7; крепление: анкер химический, 4 точки
ДК11	Замиокулькас в напольном кашпо Ø360; 400×400 мм			аналог по характеристикам	шт.	1		пом. 7
ДК12	Картина над изголовьем: графика, паспарту, рама; 600×800 мм; низ на 1200 мм от пола			аналог по характеристикам	шт.	1	3	пом. 9; крепление: две петли на дюбелях
ДК13	Постер в раме, левый (группа «постеры»); 400×500 мм; низ на 1250 мм от пола			аналог по характеристикам	шт.	1	2	пом. 9; крепление: петля на дюбеле
ДК14	Постер в раме, средний (группа «постеры»); 400×500 мм; низ на 1250 мм от пола			аналог по характеристикам	шт.	1	2	пом. 9; крепление: петля на дюбеле
ДК15	Постер в раме, правый (группа «постеры»); 400×500 мм; низ на 1250 мм от пола			аналог по характеристикам	шт.	1	2	пом. 9; крепление: петля на дюбеле
ДК16**	Спатифиллум в напольном кашпо Ø360; 400×400 мм			аналог по характеристикам	шт.	1		пом. 9
ДК17	Зеркало над раковиной П9, влагостойкое; 500×700 мм; низ на 1150 мм от пола			аналог по характеристикам	шт.	1	4	пом. 10; крепление: зеркалодержатели, 4 точки
ДК20**	Картина: тёмная лиловая абстракция, холст, тонкая рама; 800×600 мм; низ на 1300 мм от пола			аналог по характеристикам	шт.	1	4	пом. 11; крепление: планка на дюбелях, 2 точки
ДК21**	Ваза напольная, керамика матовая; 300×300 мм			аналог по характеристикам	шт.	1		пом. 11
ДК18	Зеркало ростовое 500×1600; 500×1600 мм; низ на 250 мм от пола			аналог по характеристикам	шт.	1	12	пом. 12; крепление: анкер химический, 4 точки + опора снизу
ДК19	Лавр благородный в напольном кашпо Ø380; 400×400 мм			аналог по характеристикам	шт.	1		пом. 13

Допущения и предложения на листе

Основа листа: размеры сняты с размерных цепочек растрового скана плана заказчика, на объекте не замерены; ступени наружного контура приведены к граням помещений модели (ИЗ-8, К-20, К-21); высота потолка 2700 мм принята, источника нет (К-24); тип дома и перекрытие (монолит, плита 220 мм) приняты, источника нет (К-3); толщины стен приняты (250 и 120 мм), источника нет (К-21); мощность 15 кВт принята, технических условий нет (К-25).

Знак «**» — предложение проектировщика, заказчиком не утверждено (согласовать с заказчиком): ИЗ-1: ДК16 — место перенесено (9900; 6100) → (10200; 4300), основание в данных не записано; ИЗ-7: ДК20, ДК21.

См. лист открытых вопросов (лист 6, запись К-3; лист 7, записи К-20, К-21, К-24, К-25; лист 9, записи ИЗ-1, ИЗ-7; лист 10, запись ИЗ-8).

Изм.	Кол.уч	Лист	№ док.	Подп.	Дата
Разраб.		Кырлан А.С.			21.10.26
Пров.					
ГИП		Кырлан А.С.			21.10.26
Н. контр.					
Утв.					

ГД-2026-004-АИ

Четырёхкомнатная квартира

Общая площадь 102,67* м² · * размеры со скана, не замерены (реестр — л. 6–11, ИЗ-8, К-20, К-21)

Дизайн-проект интерьера четырёхкомнатной квартиры

Стадия	Лист	Листов
РП	28	124

Спецификация мебели и оборудования (продолжение)
М б/м

Кырлан Александр Сергеевич

03

Электрооборудование

Кырлан Александр Сергеевич

выпуск 05.10.2026 · 7e7a2cd217 · стр. 33 из 168

План розеток и электровыводов

Розетки, выводы кабеля, щит · размеры в мм · высоты от чистого пола

ПРЕДВАРИТЕЛЬНО · не для производства работ · открыто пунктов: 30 (реестр — л. 6–11)

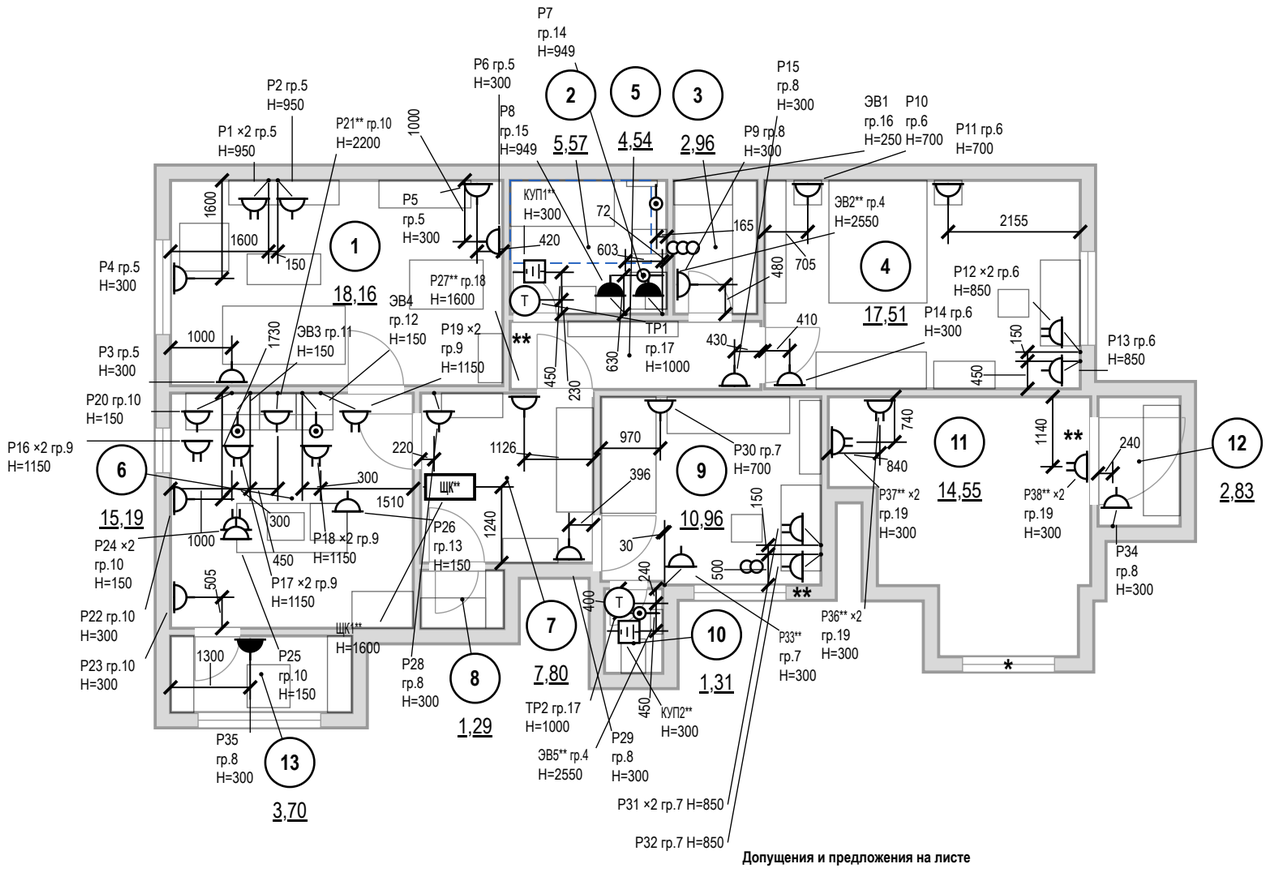

Условные обозначения

- розетка с заземляющим контактом; у знака — марка, ×N постов в рамке, гр. — группа щита, Н — высота оси, мм
- то же, рамка на 2 поста (число черточек — число постов)
- розетка влагозащищённая IP44
- вывод кабеля для подключения прибора (без розетки), марка ЭВ
- КУП — коробка уравнивания потенциалов (ДСУП), проводник к шине РЕ щита
- ЩК — щит квартирный
- Т — терморегулятор тёплого пола
- знак разведён для читаемости: точка на стене — у выноски, привязка — до неё
- граница зоны 2 ванной (600 мм от ванны/поддона)
- мебель и сантехприборы — подложка
- стояк: К1 — канализация, В1 — ХВС, Т3 — ГВС
- 1 — номер помещения, площадь м²

Допущения и предложения на листе

Основа листа: размеры сняты с размерных цепочек растрового скана плана заказчика, на объекте не замерены; ступени наружного контура приведены к граням помещений модели (ИЗ-8, К-20, К-21); высота потолка 2700 мм принята, источника нет (К-24); тип дома и перекрытие (монолит, плита 220 мм) приняты, источника нет (К-3); толщины стен приняты (250 и 120 мм), источника нет (К-21); мощность 15 кВт принята, технических условий нет (К-25).

Знак «*» — принято, не замерено и не подтверждено (замерить на объекте): К-1, К-15: Ст К1-2, Ст В1-2; К-22: окно пом. 11 (стена В).

Знак «**» — предложение проектировщика, заказчиком не утверждено (согласовать с заказчиком): ИЗ-1, К-1: окно пом. 9 (стена В); ИЗ-5: ЩК1; Р36, Р37, Р38 — перенесена из группы 9 (фартук кухни) в новую группу 19 «розетки гостиной» (EL-52: в группе 9 было бы 14 гнёзд при пределе 12); ЩК — щит ЩРВ-П-72 вместо ЩРВ-П-54: резерв при 44 занятых модулях был меньше 20 %; ИЗ-6: дверь пом. 12 (стена Г); ИЗ-8: Р33; дверь пом. 2 (стена В) — смещение 100 → 110 мм (откос до угла был 40 мм при норме от 50 мм); ИЗ-8, К-23: Р27 — высота 1600 мм выше нормы 1 м (ПУЭ 6.6.30) по назначению: питание слаботочного щита ЩС, рядом со щитом на его высоте; место сдвинуто (ИЗ-8); ИЗ-10, К-23: Р21 — высота 2200 мм выше нормы 1 м (ПУЭ 6.6.30) по назначению: питание вытяжки М25, розетка в модуле за съёмной панелью; ИЗ-12: ЭВ2, ЭВ5 — вывод к бытовому вентилятору, таймер выбега; КУП1, КУП2 — коробка уравнивания потенциалов, проводник от шины РЕ.

Открытые вопросы и конфликты по листу: К-6, К-23.

Изменения по листу без подписи: ИЗ-5, ИЗ-8–ИЗ-10.

См. лист открытых вопросов (лист 6, записи К-1, К-3, К-6; лист 7, записи К-15, К-20–К-25; лист 9, записи ИЗ-1, ИЗ-5, ИЗ-6; лист 10, записи ИЗ-8–ИЗ-10, ИЗ-12).

Примечания

1. За отметку 0,000 принят уровень чистого пола. Высоты Н — от чистого пола до оси изделия; привязки — от чистовой грани стены до оси механизма (у рамки на несколько постов — до оси рамки).
2. Высота установки, не указанная на плане: розетки — 300 мм от чистого пола; выводы кабеля — по паспорту прибора.
3. Розетки в санузле — только вне зон 0–2 (ПУЭ 7.1.48, ГОСТ Р 50571.7.701-2024), IP44, через УЗО 30 мА.
4. Розеточные и мокрые линии — через УЗО или дифавтомат с током утечки не более 30 мА (ПУЭ 7.1.79); в санузле выполнить ДСУП (ПУЭ 7.1.87–7.1.88).
5. Кабель — медный, исполнение нг(А)-LS (ГОСТ 31565-2012); скрытая прокладка только горизонтально и вертикально, фактические трассы зафиксировать исполнительной схемой до закрытия отделкой.
6. Расчёт нагрузок, токов КЗ, селективности и сечений — по проекту ЭОМ организации с допуском СРО; лист задаёт состав, расположение и группы.
7. Допущение проекта: розетки Р7 и Р8 в ванной комнате: принята норма ПУЭ 7.1.48 — зона 3, вне зон 0–2, через УЗО 30 мА, решение автора (ИЗ-19); британская норма BS 7671 (дальше 2,5 м от зоны 1) не применяется, отступление принято сознательно.
8. Ведомости электроточек, изделий, светильников и расшифровка клавиш — лист 32.

1000 мм · печать 1:1

Изм.	Кол.уч	Лист	№ док.	Подп.	Дата
Разраб.		Кырлан А.С.			21.10.26
Пров.					
ГИП		Кырлан А.С.			21.10.26
Н. контр.					
Утв.					

ГД-2026-004-АИ

Четырёхкомнатная квартира

Общая площадь 102,67* м² · * размеры со скана, не замерены (реестр — л. 6–11, ИЗ-8, К-20, К-21)

Дизайн-проект интерьера четырёхкомнатной квартиры

Стадия	Лист	Листов
РП	29	124

План розеток и электровыводов

М 1:100

Кырлан Александр Сергеевич

выпуск 05.10.2026 № 7e7a2cd217 · стр. 34 из 168

План освещения

Светильники, группы включения, извещатели · размеры в мм

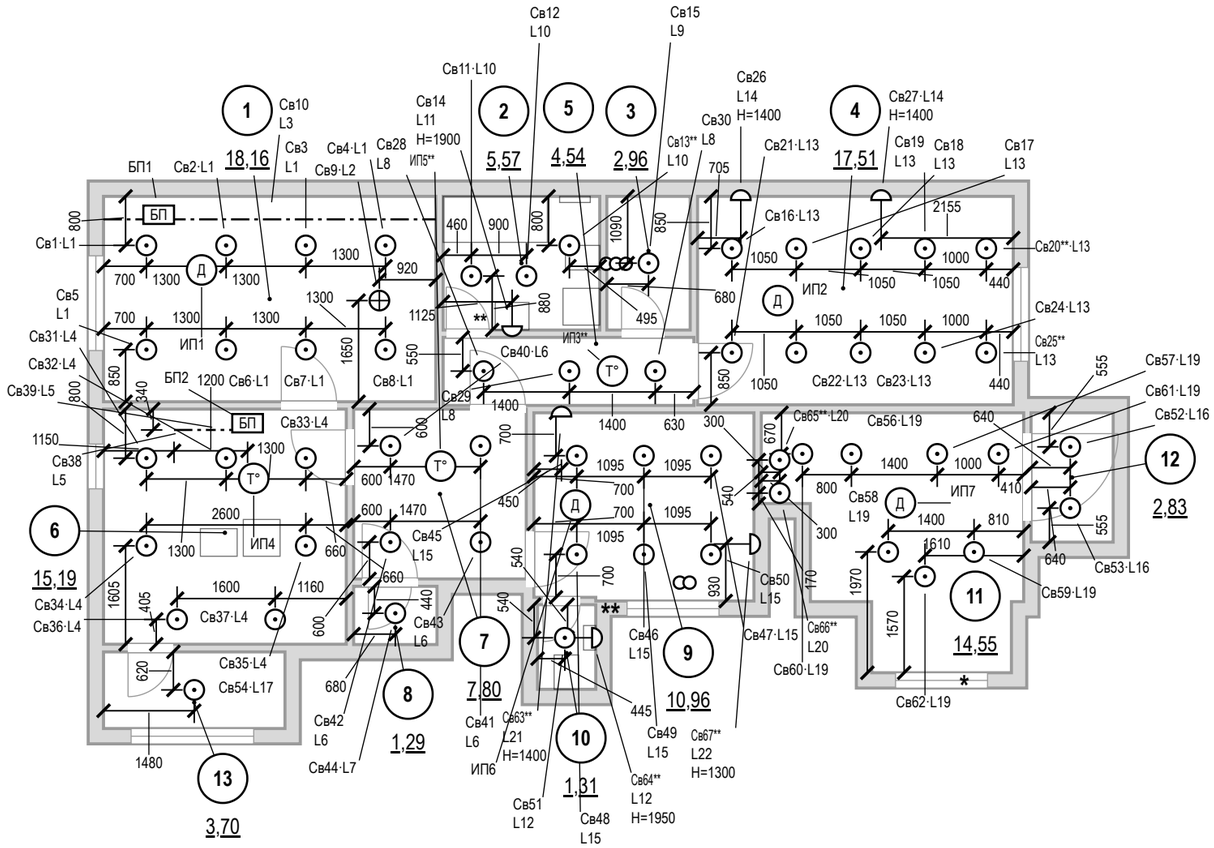

Условные обозначения

- светильник встраиваемый точечный
- светильник подвесной
- светильник настенный (бра), H — высота оси
- светодиодная лента в профиле / в карнизе короба
- Св1·L1 — марка светильника (как в ведомости и на развёртках) · группа включения L (лист выключателей)
- Д — извещатель пожарный дымовой автономный
- Т° — извещатель пожарный тепловой
- БП — блок питания LED, с доступом (люк от 100×100 мм)
- 1 — номер помещения, площадь м²

Освещённость (оценка)

Пом.	S, м²	Ен, лк	Ф треб., лм	Ф по пр., лм
1	18,2	150	7670	8000
2	5,6	50	780	1500
3	3	30	250	500
4	17,5	200	9860	10000
5	4,5	50	640	1200
6	15,2	150	6420	7000
7	7,8	50	1100	2000
8	1,3	75	270	500
9	11	200	6170	6600
10	1,3	50	180	500
11	14,6	150	6150	7000
12	2,8	75	600	1000

Допущения и предложения на листе

Основа листа: размеры сняты с размерных цепочек растрового скана плана заказчика, на объекте не замерены; ступени наружного контура приведены к граням помещений модели (ИЗ-8, К-20, К-21); высота потолка 2700 мм принята, источника нет (К-24); тип дома и перекрытие (монолит, плита 220 мм) приняты, источника нет (К-3); толщины стен приняты (250 и 120 мм), источника нет (К-21); мощность 15 кВт принята, технических условий нет (К-25).

Знак «*» — принято, не замерено и не подтверждено (замерить на объекте): К-1, К-15: Ст К1-2, Ст В1-2; К-22: окно пом. 11 (стена В).

Знак «**» — предложение проектировщика, заказчиком не утверждено (согласовать с заказчиком): ИЗ-1, К-1: окно пом. 9 (стена В); ИЗ-2: Св63, Св67; ИЗ-3: Св64; ИЗ-6: дверь пом. 12 (стена Г); ИЗ-7: Св65, Св66; ИЗ-8: Св13, Св20, Св25, ИП3, ИП5; дверь пом. 2 (стена В) — смещение 100 → 110 мм (откос до угла был 40 мм при норме от 50 мм).

Изменения по листу без подписи: ИЗ-7–ИЗ-9.

См. лист открытых вопросов (лист 6, записи К-1, К-3; лист 7, записи К-15, К-20–К-22, К-24, К-25; лист 9, записи ИЗ-1–ИЗ-3, ИЗ-6, ИЗ-7; лист 10, записи ИЗ-8, ИЗ-9).

Примечания

1. За отметку 0,000 принят уровень чистого пола. Высоты H — от чистого пола до оси изделия; привязки — от чистовой грани стены до оси механизма (у рамки на несколько постов — до оси рамки).
2. Высота установки, не указанная на плане: светильники — на потолке; настенные — по отметке H у знака. Привязки — до оси светильника от чистовой грани стены, по рядам.
3. Освещённость: Ен — СанПиН 1.2.3685-21, табл. 5.52 (на полу); Ф треб. = Ен·S/(U·MF) при U = 0,5 и MF = 0,71 (СП 52.13330.2016, табл. 4.3) — оценка, не светотехнический расчёт. Декоративная подсветка в Ф не входит.
4. Во влажных помещениях — светильники не ниже IP44; в зонах 0–2 ванной — по ГОСТ Р 50571.7.701-2024 (зона 1 — IPX5).
5. LED-лента в карнизе подсветки короба — по линии карниза с плана потолков; блок питания — в люке короба (БП на плане), питание ленты длиннее 5 м — с двух концов.
6. Розеточные и мокрые линии — через УЗО или дифавтомат с током утечки не более 30 мА (ПУЭ 7.1.79); в санузле выполнить ДСУП (ПУЭ 7.1.87–7.1.88).
7. Кабель — медный, исполнение нг(A)-LS (ГОСТ 31565-2012); скрытая прокладка только горизонтально и вертикально, фактические трассы зафиксировать исполнительной схемой до закрытия отделкой.
8. Расчёт нагрузок, токов КЗ, селективности и сечений — по проекту ЭОМ организации с допуском СРО; лист задаёт состав, расположение и группы.
9. Ведомость светильников — лист 32.

1000 мм · печать 1:1

Изм.	Кол.уч	Лист	№ док.	Подп.	Дата
Разраб.		Кырлан А.С.			21.10.26
Пров.					
ГИП		Кырлан А.С.			21.10.26
Н. контр.					
Утв.					

ГД-2026-004-АИ

Четырёхкомнатная квартира

Общая площадь 102,67* м² · * размеры со скана, не замерены (реестр — л. 6–11, ИЗ-8, К-20, К-21)

Дизайн-проект интерьера четырёхкомнатной квартиры

Стадия	Лист	Листов
РП	30	124

План освещения

М 1:100

Кырлан Александр Сергеевич

выпуск 05.10.2026 № 7e7a2cd217 · стр. 35 из 168

План выключателей и схема включения

Выключатели S, группы включения L, линии связи · размеры в мм

ПРЕДВАРИТЕЛЬНО · не для производства работ · открыто пунктов: 30 (реестр — л. 6–11)

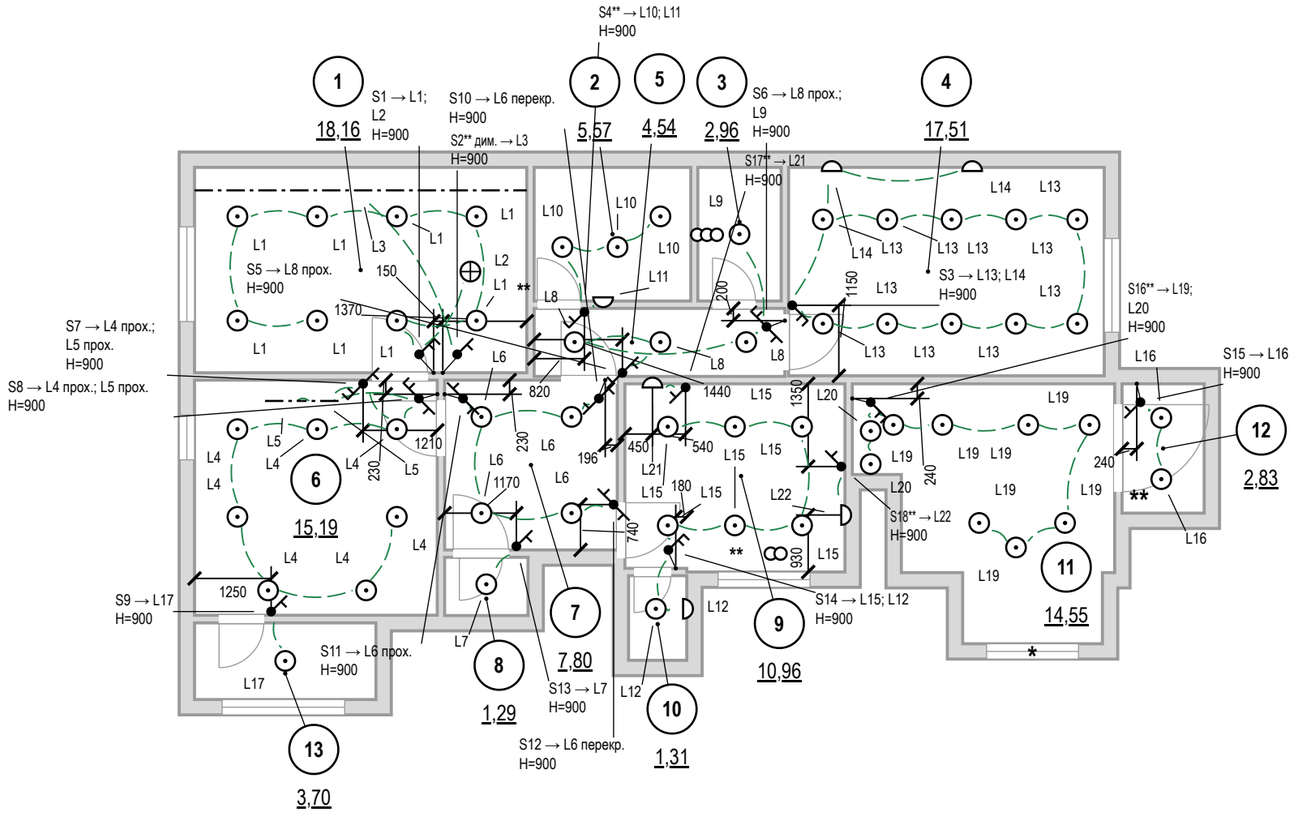

Условные обозначения

- выключатель одноклавишный
- выключатель двухклавишный (флажков — по числу клавиш)
- выключатель с проходной или перекрёстной клавишей (обратный флажок); тип клавиши — в подписи
- S1 → — марка → группы по клавишам (через «;»): прох. — проходной, перекр. — перекрёстный, дим. — светорегулятор; Н — высота
- линия связи: выключатель → светильники группы (не трасса кабеля)
- светильник встраиваемый точечный
- светильник подвесной
- светильник настенный (бра), Н — высота оси
- светодиодная лента в профиле / в карнизе короба
- L1 — группа включения у светильника
- (1) — номер помещения, площадь м²

Допущения и предложения на листе

Основа листа: размеры сняты с размерных цепочек растрового скана плана заказчика, на объекте не замерены; ступени наружного контура приведены к граням помещений модели (ИЗ-8, К-20, К-21); высота потолка 2700 мм принята, источника нет (К-24); тип дома и перекрытие (монолит, плита 220 мм) приняты, источника нет (К-3); толщины стен приняты (250 и 120 мм), источника нет (К-21); мощность 15 кВт принята, технических условий нет (К-25).

Знак «*» — принято, не замерено и не подтверждено (замерить на объекте): К-1, К-15: Ст К1-2, Ст В1-2; К-22: окно пом. 11 (стена В).

Знак «**» — предложение проектировщика, заказчиком не утверждено (согласовать с заказчиком): ИЗ-1, К-1: окно пом. 9 (стена В); ИЗ-2: S17, S18; ИЗ-4: S2 — светорегулятор добавлен под диммируемую ленту L3; уровни сценариев выбраны конвейером; ИЗ-6: дверь пом. 12 (стена Г); ИЗ-7: S16 — вторая клавиша (подсветка картины ДК20) добавлена как предложение; ИЗ-8: S4; дверь пом. 2 (стена В) — смещение 100 → 110 мм (откос до угла был 40 мм при норме от 50 мм).

Изменения по листу без подписи: ИЗ-7.

См. лист открытых вопросов (лист 6, записи К-1, К-3; лист 7, записи К-15, К-20–К-22, К-24, К-25; лист 9, записи ИЗ-1, ИЗ-2, ИЗ-4, ИЗ-6, ИЗ-7; лист 10, запись ИЗ-8).

Примечания

1. За отметку 0,000 принят уровень чистого пола. Высоты Н — от чистого пола до оси изделия; привязки — от чистовой грани стены до оси механизма (у рамки на несколько постов — до оси рамки).
2. Высота установки, не указанная на плане: выключатели — 900 мм от чистого пола, со стороны дверной ручки (ПУЭ 7.1.51).
3. Линии связи показывают, какой выключатель какую группу L включает; это не трасса кабеля. Трасса — принципиальная, фактическую зафиксировать исполнительной схемой.
4. Группы из нескольких мест (L8 — S5, S6; L4 — S7, S8; L5 — S7, S8; L6 — S10, S11, S12): на крайних местах — проходные клавиши, на промежуточных перекрёстные; механизмы — в ведомости изделий.
5. Светорегулятор — по заднему фронту (для LED-драйверов), совместимость с драйверами проверить до закупки.
6. Розеточные и мокрые линии — через УЗО или дифавтомат с током утечки не более 30 мА (ПУЭ 7.1.79); в санузле выполнить ДСУП (ПУЭ 7.1.87–7.1.88).
7. Кабель — медный, исполнение нг(А)-LS (ГОСТ 31565-2012); скрытая прокладка только горизонтально и вертикально, фактические трассы зафиксировать исполнительной схемой до закрытия отделкой.
8. Расчёт нагрузок, токов КЗ, селективности и сечений — по проекту ЭОМ организации с допуском СРО; лист задаёт состав, расположение и группы.
9. Расшифровка клавиш и ведомость изделий — лист 32.

1000 мм · печать 1:1

Изм.	Кол.уч	Лист	№ док.	Подп.	Дата
Разраб.		Кырлан А.С.			21.10.26
Пров.					
ГИП		Кырлан А.С.			21.10.26
Н. контр.					
Утв.					

ГД-2026-004-АИ

Четырёхкомнатная квартира

Общая площадь 102,67* м² · * размеры со скана, не замерены (реестр — л. 6–11, ИЗ-8, К-20, К-21)

Дизайн-проект интерьера четырёхкомнатной квартиры

Стадия	Лист	Листов
РП	31	124

План выключателей и схема включения

М 1:100

Кырлан Александр Сергеевич

выпуск 05.10.2026 № 7e7a2cd217 · стр. 36 из 168

Ведомость электроточек и изделий

Электроточки, изделия, светильники, клавиши выключателей · б/м

Ведомость электроточек

Марка	Пом.	Назначение	H, мм	Гр.
Р1	1	ТВ-зона: телевизор, медиаплеер	950	5
Р2	1	ТВ-зона: саундбар	950	5
Р3	1	торшер у дивана М2	300	5
Р4	1	кресло у окна М4	300	5
Р5	1	обеденная зона, буфет М6	300	5
Р6	1	уборка	300	5
КУП1**	2	КУП — коробка уравнивания потенциалов (ДСУП)	300	
Р7	2	стиральная машина, IP44	949	14
Р8	2	фен у умывальника, IP44	949	15
ТР1	2	терморегулятор тёплого пола ванной, IP44	1000	17
ЭВ1	2	полотенцесушитель электрический П5, IP44	250	16
ЭВ2**	2	вентилятор ВР1 (таймер выбега), IP44	2550	4
Р9	3	уборка, пылесос	300	8
Р10	4	у кровати, тумба М12	700	6
Р11	4	у кровати, тумба М13	700	6
Р12	4	рабочий стол М14	850	6
Р13	4	рабочий стол М14	850	6
Р14	4	уборка	300	6
Р15	5	уборка	300	8
Р16	6	фартук: мелкая техника	1150	9
Р17	6	фартук: мелкая техника	1150	9
Р18	6	фартук: мелкая техника	1150	9
Р19	6	фартук: мелкая техника	1150	9
Р20	6	холодильник встроенный М20 (розетка в модуле М21)	150	10
Р21**	6	вытяжка М25 (в модуле, съёмная панель)	2200	10
Р22	6	кухня: мелкая техника	300	10
Р23	6	уборка	300	10
Р24	6	торцевая панель острова М27: мелкая техника	150	10
Р25	6	торцевая панель острова М27: мелкая техника	150	10

Ведомость электроточек (продолжение)

Марка	Пом.	Назначение	H, мм	Гр.
Р26	6	посудомоечная машина в острове М27	150	13
ЭВ3	6	варочная панель М22	150	11
ЭВ4	6	духовой шкаф М22 (вывод в соседнем модуле М23)	150	12
Р27**	7	слаботочный щит ЩС**: роутер, ONT	1600	18
Р28	7	уборка	300	8
Р29	7	уборка	300	8
ЩК1**	7	квартирный щит ЩК**, 72 модуля	1600	
Р30	9	у кровати М34	700	7
Р31	9	рабочий стол М36*	850	7
Р32	9	рабочий стол М36*	850	7
Р33**	9	уборка	300	7
КУП2**	10	КУП — коробка уравнивания потенциалов (ДСУП)	300	
ТР2	10	терморегулятор тёплого пола санузла, IP44	1000	17
ЭВ5**	10	вентилятор ВР3 (таймер выбега), IP44	2550	4
Р36**	11	розетка общего назначения	300	19
Р37**	11	розетка общего назначения	300	19
Р38**	11	розетка общего назначения	300	19
Р34	12	уборка, отпариватель	300	8
Р35	13	балкон: розетка общего назначения, IP44	300	8

Ведомость изделий

Наименование	Марки	Ед.	Кол.
Розетка с з/к и защитными шторками, 16 А	по ведомости точек	шт	46
Розетка IP44 с крышкой, 16 А	Р7, Р8, Р35	шт	3
Выключатель 1-клав.	S9, S13, S15, S17**, S18**	шт	5
Выключатель 1-клав. перекрёстный	S10, S12	шт	2
Выключатель 1-клав. проходной	S5, S11	шт	2
Выключатель 2-клав.	S1, S3, S4**, S14, S16**	шт	5
Выключатель 2-клав. (проходная + обычная)	S6	шт	1

Ведомость изделий (продолжение)

Наименование	Марки	Ед.	Кол.
Выключатель 2-клав. проходной	S7, S8	шт	2
Светорегулятор 1-канальный, задний фронт (LED)	S2**	шт	1
Рамка 1-постовая	в т. ч. 18 под выключ.	шт	45
Рамка 2-постовая		шт	11
Терморегулятор тёплого пола	ТР1, ТР2	шт	2
Коробка установочная (подрозетник) Ø68	розетки, выключатели	шт	69
Вывод кабеля под прибор (клеммник)	ЭВ1, ЭВ2**, ЭВ3, ЭВ4, ЭВ5**	шт	5
Коробка уравнивания потенциалов КУП	КУП1**, КУП2**	шт	2
Блок питания LED 24 В, 100 Вт, дим.	БП1	шт	1
Блок питания LED 24 В, 30 Вт	БП2	шт	1
Извещатель дымовой автономный	ИП1, ИП2, ИП6, ИП7	шт	4
Извещатель тепловой	ИП3**, ИП4, ИП5**	шт	3
Щит квартирный (состав — лист щита)	ЩК1**	шт	1
Розетка компьютерная RJ45, кат. 6, с рамкой и подрозетником	LAN1–LAN3, LAN4**	шт	4
Розетка телевизионная (коаксиальная) с рамкой и подрозетником	ТВ1	шт	1
Точка доступа Wi-Fi (оборудование заказчика), питание PoE	AP1**, AP2**	шт	2
Щит слаботочный ЩС**: корпус, DIN-рейка, розетки 220 В	ЩС**	шт	1
Патч-панель, портов не менее 6		шт	1
Коммутатор, портов не менее 6, из них PoE 2		шт	1
Кабель коаксиальный RG-6 (75 Ом) к розеткам ТВ (по лучам от ЩС**, запас 10 %)		м	14,5
Кабель U/UTP кат. 6 (LAN, Wi-Fi и камеры по PoE) (по лучам от ЩС**, запас 10 %)		м	70,7

Ведомость светильников

Поз.	Марки	Тип	Кол.	P, Вт	Ф, лм	IP	Тц/Ra
1	Св1–Св8, Св16–Св19, Св20**, Св21–Св24, Св25**, Св31–Св37, Св56–Св62	встраиваемый точечный	32	12	1000		3000/90
2	Св9	подвесной	1	15	1200		2700/90
3	Св10	светодиодная лента, 5,4 м	1	51,8	4860		2700/90
4	Св11, Св12, Св13**, Св51	встраиваемый точечный	4	6	500	44	3000/90
5	Св14, Св64**	настенный (бра), H=1900	2	8	600	44	3000/90
6	Св15, Св40–Св44, Св52, Св53, Св65**, Св66**	встраиваемый точечный	10	6	500		3000/90
7	Св26, Св27, Св63**	настенный (бра), H=1400	3	6	400		2700/90
8	Св28–Св30	встраиваемый точечный	3	5	400		3000/90
9	Св38, Св39	линейный светильник	2	8	700		3000/90
10	Св45–Св50	встраиваемый точечный	6	13	1100		3000/90
11	Св67**	настенный (бра), H=1300	1	7	450		3000/90
12	Св54	встраиваемый точечный	1	9	800	44	3000/90

Расшифровка клавиш

Марка	Пом.	H, мм	Клав.	Механизм	Группа: светильники
S1	1	900	1	обычный	L1: Св1–Св8
			2	обычный	L2: Св9
S2**	1	900	1	светорегулятор	L3: Св10
S3	4	900	1	обычный	L13: Св16–Св19, Св20**, Св21–Св24, Св25**
			2	обычный	L14: Св26, Св27
S4**	5	900	1	обычный	L10: Св11, Св12, Св13**
			2	обычный	L11: Св14
S5	5	900	1	проходной	L8: Св28–Св30
S6	5	900	1	проходной	L8: Св28–Св30
			2	обычный	L9: Св15

Примечания

1. Ведомости сведены с планов розеток, освещения и выключателей; марки, группы и высоты — те же, что у знаков на планах.
2. Механизмы, рамки и светорегуляторы — одной серии; число постов и клавиш сверено с выбранной серией. Перекрёстная клавиша — отдельный механизм серии.
3. За отметку 0,000 принят уровень чистого пола. Высоты H — от чистого пола до оси изделия; привязки — от чистовой грани стены до оси механизма (у рамки на несколько постов — до оси рамки).
4. Розеточные и мокрые линии — через УЗО или дифавтомат с током утечки не более 30 мА (ПУЭ 7.1.79); в санузле выполнить ДСУП (ПУЭ 7.1.87–7.1.88).
5. Кабель — медный, исполнение нг(A)-LS (ГОСТ 31565-2012); скрытая прокладка только горизонтально и вертикально, фактические трассы зафиксировать исполнительной схемой до закрытия отделкой.
6. Расчёт нагрузок, токов КЗ, селективности и сечений — по проекту ЭОМ организации с допуском СРО; лист задаёт состав, расположение и группы.
7. Допущение проекта: розетки Р7 и Р8 в ванной комнате: принята норма ПУЭ 7.1.48 — зона 3, вне зон 0–2, через УЗО 30 мА, решение автора (ИЗ-19); британская норма BS 7671 (дальше 2,5 м от зоны 1) не применяется, отступление принято сознательно.
8. Ведомости занимают 2 листов этого наименования: таблицы, не вошедшие в поле листа, продолжены на следующем листе.

Допущения и предложения на листе. Знак «*» принято (замерить). Знак «**» предложено (согласовать). См. лист открытых вопросов (листы 6–11).

Изм.	Кол.уч	Лист	№ док.	Подп.	Дата
Разраб.		Кырлан А.С.			21.10.26
Пров.					
ГИП		Кырлан А.С.			21.10.26
Н. контр.					
Утв.					

ГД-2026-004-АИ

Четырёхкомнатная квартира

Общая площадь 102,67* м² · * размеры со скана, не замерены (реестр — л. 6–11, ИЗ-8, К-20, К-21)

Дизайн-проект интерьера четырёхкомнатной квартиры

Стадия	Лист	Листов
РП	32	124

Ведомость электроточек и изделий

М б/м

Кырлан Александр Сергеевич

Ведомость электроточек и изделий (продолжение)

Электроточки, изделия, светильники, клавиши выключателей · б/м

Расшифровка клавиш (продолжение)

Марка	Пом.	Н, мм	Клав.	Механизм	Группа: светильники
S7	6	900	1	проходной	L4: Св31–Св37
			2	проходной	L5: Св38, Св39
S8	6	900	1	проходной	L4: Св31–Св37
			2	проходной	L5: Св38, Св39
S9	6	900	1	обычный	L17: Св54
S10	7	900	1	перекрёстный	L6: Св40–Св43
S11	7	900	1	проходной	L6: Св40–Св43
S12	7	900	1	перекрёстный	L6: Св40–Св43
S13	7	900	1	обычный	L7: Св44
S14	9	900	1	обычный	L15: Св45–Св50
			2	обычный	L12: Св51, Св64**
S15	12	900	1	обычный	L16: Св52, Св53
S16**	11	900	1	обычный	L19: Св56–Св62
			2	обычный	L20: Св65**, Св66**
S17**	9	900	1	обычный	L21: Св63**
S18**	9	900	1	обычный	L22: Св67**

Допущения и предложения на листе

Основа листа: размеры сняты с размерных цепочек растрового скана плана заказчика, на объекте не замерены; ступени наружного контура приведены к граням помещений модели (ИЗ-8, К-20, К-21); высота потолка 2700 мм принята, источника нет (К-24); тип дома и перекрытие (монолит, плита 220 мм) приняты, источника нет (К-3); толщины стен приняты (250 и 120 мм), источника нет (К-21); мощность 15 кВт принята, технических условий нет (К-25).

Знак «**» — предложение проектировщика, заказчиком не утверждено (согласовать с заказчиком): ИЗ-2: S17, Св63, S18, Св67; ИЗ-3: Св64; ИЗ-7: S16 — вторая клавиша (подсветка картины ДК20) добавлена как предложение; Св65, Св66.

Открытые вопросы и конфликты по листу: К-23.

Изменения по листу без подписи: ИЗ-5, ИЗ-10.

См. лист открытых вопросов (лист 6, запись К-3; лист 7, записи К-20, К-21, К-23–К-25; лист 9, записи ИЗ-2, ИЗ-3, ИЗ-5, ИЗ-7; лист 10, записи ИЗ-8, ИЗ-10).

Примечания

1. Продолжение ведомостей: лист 2 из 2 этого наименования; таблицы, прерванные на предыдущем листе, продолжены с заголовком «(продолжение)».
2. За отметку 0,000 принят уровень чистого пола. Высоты Н — от чистого пола до оси изделия; привязки — от чистовой грани стены до оси механизма (у рамки на несколько постов — до оси рамки).
3. Розеточные и мокрые линии — через УЗО или дифавтомат с током утечки не более 30 мА (ПУЭ 7.1.79); в санузле выполнить ДСУП (ПУЭ 7.1.87–7.1.88).
4. Кабель — медный, исполнение нг(А)-LS (ГОСТ 31565-2012); скрытая прокладка только горизонтально и вертикально, фактические трассы зафиксировать исполнительной схемой до закрытия отделкой.
5. Расчёт нагрузок, токов КЗ, селективности и сечений — по проекту ЭОМ организации с допуском СРО; лист задаёт состав, расположение и группы.

Изм.	Кол.уч	Лист	№ док.	Подп.	Дата
Разраб.		Кырлан А.С.			21.10.26
Пров.					
ГИП		Кырлан А.С.			21.10.26
Н. контр.					
Утв.					

ГД-2026-004-АИ

Четырёхкомнатная квартира

Общая площадь 102,67* м² · * размеры со скана, не замерены (реестр — л. 6–11, ИЗ-8, К-20, К-21)

Дизайн-проект интерьера четырёхкомнатной квартиры

Стадия	Лист	Листов
РП	33	124

Ведомость электроточек и изделий (продолжение)
М б/м

Кырлан Александр Сергеевич

выпуск 05.10.2026 № 7e7a2cd217 · стр. 38 из 168

Однолинейная схема щита

Щит квартирный ЩК** · гр. 1—10 из 19 · без масштаба

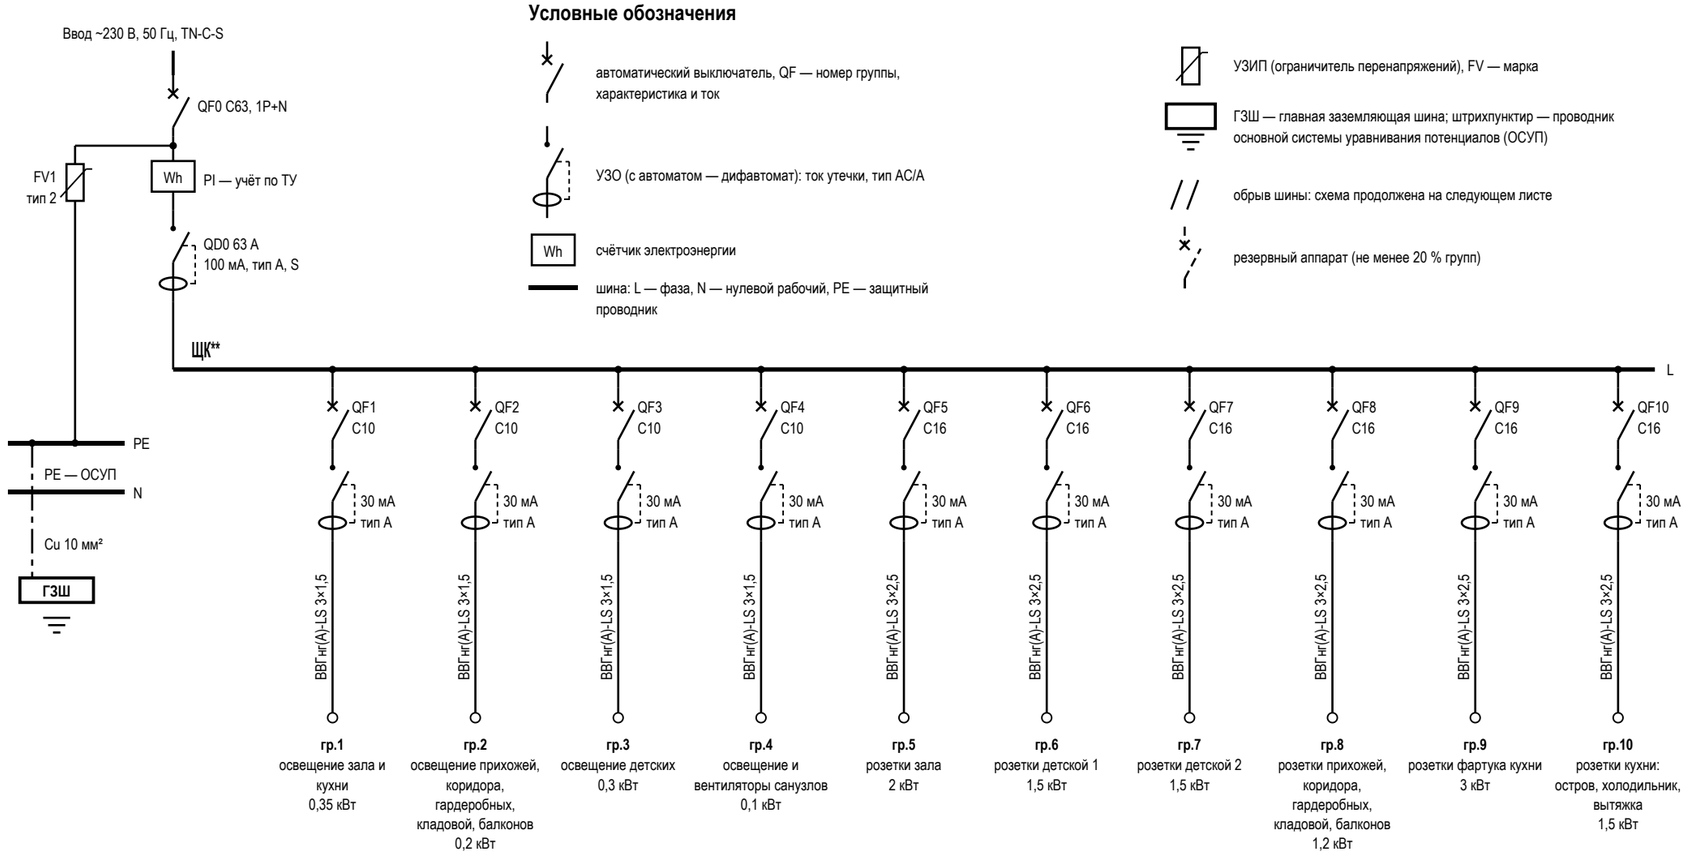

Условные обозначения

- автоматический выключатель, QF — номер группы, характеристика и ток
- УЗО (с автоматом — дифавтомат): ток утечки, тип AC/A
- Wh — счётчик электроэнергии
- шина: L — фаза, N — нулевой рабочий, PE — защитный проводник
- УЗИП (ограничитель перенапряжений), FV — марка
- ГЗШ — главная заземляющая шина; штрихпунктир — проводник основной системы уравнивания потенциалов (ОСУП)
- обрыв шины: схема продолжена на следующем листе
- резервный аппарат (не менее 20 % групп)

Данные щитка

Показатель	Значение
Номер щитка	ЩК**
Тип	ЩРВ-П-72, IP41, навесной
Уст. мощность, кВт	29,75
Разреш. мощность, кВт	15
Расчётная, кВт	11,2
Автоматы 1п: занят. / рез.	19 / 4
Модулей: всего / занято	72 / 44
Ток на вводе, А	63
Вводной аппарат	QF0 C63, 1P+N
УЗИП	FV1, тип 2, ЩК**, после счётчика
ГЗШ, проводник ОСУП	Cu 10 мм²
Листов схемы	2 (группы по листам)

Таблица групп щита ЩК** и кабельный журнал

№	Назначение	Помещения	Автомат	УЗО / дифавтомат	Кабель	Длина, м	Р, кВт	Точек
1	освещение зала и кухни	1, 6	C10	30 мА, тип A	ВВГнг(A)-LS 3×1,5	42	0,35	25
2	освещение прихожей, коридора, гардеробных, кладовой, балконов	3, 5, 6, 7, 8, 12, 13	C10	30 мА, тип A	ВВГнг(A)-LS 3×1,5	48	0,2	20
3	освещение детских	4, 9, 11	C10	30 мА, тип A	ВВГнг(A)-LS 3×1,5	38	0,3	34
4	освещение и вентиляторы санузлов	2, 5, 10	C10	30 мА, тип A	ВВГнг(A)-LS 3×1,5	26	0,1	9
5	розетки зала	1	C16	30 мА, тип A	ВВГнг(A)-LS 3×2,5	34	2	6
6	розетки детской 1	4	C16	30 мА, тип A	ВВГнг(A)-LS 3×2,5	36	1,5	5
7	розетки детской 2	9	C16	30 мА, тип A	ВВГнг(A)-LS 3×2,5	30	1,5	4
8	розетки прихожей, коридора, гардеробных, кладовой, балконов	3, 5, 7, 12, 13	C16	30 мА, тип A	ВВГнг(A)-LS 3×2,5	48	1,2	6
9	розетки фартука кухни	6	C16	30 мА, тип A	ВВГнг(A)-LS 3×2,5	22	3	4
10	розетки кухни: остров, холодильник, вытяжка	6	C16	30 мА, тип A	ВВГнг(A)-LS 3×2,5	26	1,5	6

Примечания

1. Схема однолинейная: одна линия — фаза, N и PE группы; аппараты — в отключённом положении (ГОСТ 2.702, ГОСТ 2.755). Номера групп — как у точек на планах (гр.). За отметку 0,000 принят уровень чистого пола; высота щита — по плану розеток.
2. Розеточные и мокрые линии — через УЗО или дифавтомат с током утечки не более 30 мА (ПУЭ 7.1.79); в санузле выполнить ДСУП (ПУЭ 7.1.87–7.1.88).
3. УЗО тип A — для линий с электроникой, стиральной и посудомоечной машиной, LED-драйверами; тип AC — только для чисто активной нагрузки.
4. Кабель — медный, исполнение нг(A)-LS (ГОСТ 31565-2012); скрытая прокладка только горизонтально и вертикально, фактические трассы зафиксировать исполнительной схемой до закрытия отделкой.
5. Номинал автомата — не выше допустимого тока кабеля: 1,5 мм² — до 10 А, 2,5 мм² — до 16 А. Резерв щита — не менее 20 % модулей.
6. Расчёт нагрузок, токов КЗ, селективности и сечений — по проекту ЭОМ организации с допуском СРО; лист задаёт состав, расположение и группы.
7. УЗИП FV1 — после вводного автомата, проводник к шине PE — кратчайший, без петель. Шина PE щита соединяется с ГЗШ проводником ОСУП; к ГЗШ присоединяются трубы водопровода и отопления на вводе в квартиру (ПУЭ 7.1.87). Шины N и PE — раздельные, после разделения PEN не объединяются.
8. До подключения нагрузки — приёмо-сдаточные испытания с протоколом: сопротивление изоляции линий не менее 0,5 МОм, срабатывание УЗО по току и времени, непрерывность защитных проводников PE (ПУЭ, гл. 1.8).

Допущения и предложения на листе

Основа листа: размеры сняты с размерных цепочек растрового скана плана заказчика, на объекте не замерены; ступени наружного контура приведены к граням помещений модели (ИЗ-8, К-20, К-21); высота потолка 2700 мм принята, источника нет (К-24); тип дома и перекрытие (монолит, плита 220 мм) приняты, источника нет (К-3); толщины стен приняты (250 и 120 мм), источника нет (К-21); мощность 15 кВт принята, технических условий нет (К-25).

Знак «**» — предложение проектировщика, заказчиком не утверждено (согласовать с заказчиком): ИЗ-5: ЩК — щит ЩРВ-П-72 вместо ЩРВ-П-54: резерв при 44 занятых модулях был меньше 20 %.

Открытые вопросы и конфликты по листу: К-25.

Изменения по листу без подписи: ИЗ-5.

См. лист открытых вопросов (лист 6, запись К-3; лист 7, записи К-20, К-21, К-24, К-25; лист 9, запись ИЗ-5; лист 10, запись ИЗ-8).

Изм.	Кол.уч	Лист	№ док.	Подп.	Дата
Разраб.		Кырлан А.С.			21.10.26
Пров.					
ГИП		Кырлан А.С.			21.10.26
Н. контр.					
Утв.					

ГД-2026-004-АИ

Четырёхкомнатная квартира

Общая площадь 102,67* м² · * размеры со скана, не замерены (реестр — л. 6–11, ИЗ-8, К-20, К-21)

Дизайн-проект интерьера четырёхкомнатной квартиры

Стадия	Лист	Листов
РП	34	124

Однолинейная схема щита

М б/м

Кырлан Александр Сергеевич

выпуск 05.10.2026 № 7e7a2cd217 · стр. 39 из 168

Однолинейная схема щита (продолжение)

Щит квартирный ЩК** · гр. 11—19 из 19 · без масштаба

Продолжение однолинейной схемы щита ЩК**, начало — лист 34

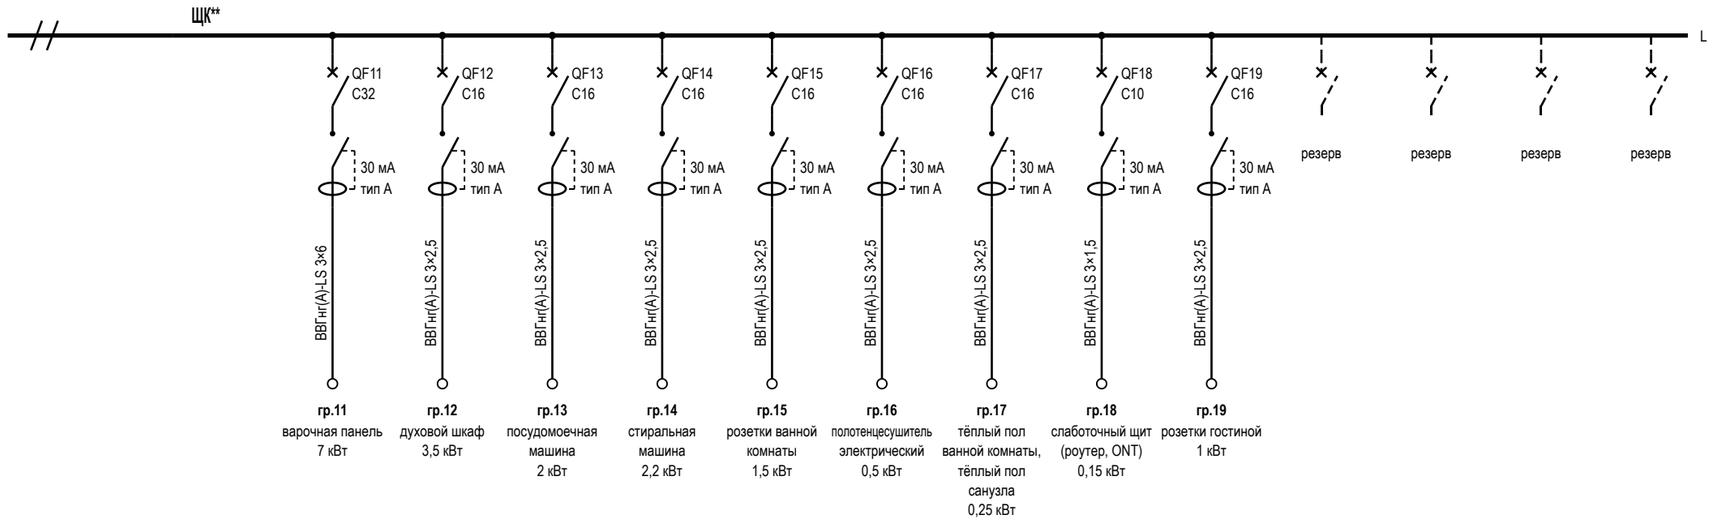

Таблица групп щита ЩК** и кабельный журнал (продолжение)

№	Назначение	Помещения	Автомат	УЗО / дифавтомат	Кабель	Длина, м	Р, кВт	Точек
11	варочная панель	6	C32	30 мА, тип A	ВВГнг(A)-LS 3×6	20	7	1
12	духовой шкаф	6	C16	30 мА, тип A	ВВГнг(A)-LS 3×2,5	20	3,5	1
13	посудомоечная машина	6	C16	30 мА, тип A	ВВГнг(A)-LS 3×2,5	22	2	1
14	стиральная машина	2	C16	30 мА, тип A	ВВГнг(A)-LS 3×2,5	17	2,2	1
15	розетки ванной комнаты	2	C16	30 мА, тип A	ВВГнг(A)-LS 3×2,5	18	1,5	1
16	полотенцесушитель электрический	2	C16	30 мА, тип A	ВВГнг(A)-LS 3×2,5	18	0,5	1
17	тёплый пол ванной комнаты, тёплый пол санузла	2, 10	C16	30 мА, тип A	ВВГнг(A)-LS 3×2,5	20	0,25	2
18	слаботочный щит (роутер, ONT)	7	C10	30 мА, тип A	ВВГнг(A)-LS 3×1,5	6	0,15	1
19	розетки гостиной	11	C16	30 мА, тип A	ВВГнг(A)-LS 3×2,5	30	1	3
	Итого по сечениям ВВГнг(A)-LS (все группы щита), м: 3×1,5 — 160; 3×2,5 — 341; 3×6 — 20					521		

Примечания

1. Лист — продолжение однолинейной схемы щита ЩК**: начало, данные щитка и условные обозначения — лист 34. Ввод, учёт, вводной аппарат, УЗИП, шины N и PE и ГЗШ показаны там же; шина L листа — та же шина щита.
2. Схема однолинейная: одна линия — фаза, N и PE группы; аппараты — в отключённом положении (ГОСТ 2.702, ГОСТ 2.755). Номера групп — как у точек на планах (гр.). За отметку 0,000 принят уровень чистого пола; высота щита — по плану розеток.
3. Розеточные и мокрые линии — через УЗО или дифавтомат с током утечки не более 30 мА (ПУЭ 7.1.79); в санузле выполнить ДСУП (ПУЭ 7.1.87–7.1.88).
4. УЗО тип A — для линий с электроникой, стиральной и посудомоечной машиной, LED-драйверами; тип AC — только для чисто активной нагрузки.
5. Кабель — медный, исполнение нг(A)-LS (ГОСТ 31565-2012); скрытая прокладка только горизонтально и вертикально, фактические трассы зафиксировать исполнительной схемой до закрытия отделкой.
6. Номинал автомата — не выше допустимого тока кабеля: 1,5 мм² — до 10 А, 2,5 мм² — до 16 А. Резерв щита — не менее 20 % модулей.
7. Расчёт нагрузок, токов КЗ, селективности и сечений — по проекту ЭОМ организации с допуском СРО; лист задаёт состав, расположение и группы.
8. До подключения нагрузки — приёмо-сдаточные испытания с протоколом: сопротивление изоляции линий не менее 0,5 МОм, срабатывание УЗО по току и времени, непрерывность защитных проводников PE (ПУЭ, гл. 1.8).

Допущения и предложения на листе

Основа листа: размеры сняты с размерных цепочек растрового скана плана заказчика, на объекте не замерены; ступени наружного контура приведены к граням помещений модели (ИЗ-8, К-20, К-21); высота потолка 2700 мм принята, источника нет (К-24); тип дома и перекрытие (монолит, плита 220 мм) приняты, источника нет (К-3); толщины стен приняты (250 и 120 мм), источника нет (К-21); мощность 15 кВт принята, технических условий нет (К-25).

Знак «**» — предложение проектировщика, заказчиком не утверждено (согласовать с заказчиком): ИЗ-5: ЩК — щит ЩРВ-П-72 вместо ЩРВ-П-54: резерв при 44 занятых модулях был меньше 20 %.

Открытые вопросы и конфликты по листу: К-25.

Изменения по листу без подписи: ИЗ-5.

См. лист открытых вопросов (лист 6, запись К-3; лист 7, записи К-20, К-21, К-24, К-25; лист 9, запись ИЗ-5; лист 10, запись ИЗ-8).

Изм.	Кол.уч	Лист	№ док.	Подп.	Дата	ГД-2026-004-АИ			
						Четырёхкомнатная квартира			
						Общая площадь 102,67* м² · * размеры со скана, не замерены (реестр — л. 6–11, ИЗ-8, К-20, К-21)			
Разраб.		Кырлан А.С.			21.10.26	Дизайн-проект интерьера четырёхкомнатной квартиры	Стадия	Лист	Листов
Пров.							РП	35	124
ГИП		Кырлан А.С.			21.10.26				
Н. контр.						Однолинейная схема щита (продолжение)	Кырлан Александр Сергеевич		
Утв.						М б/м			

выпуск 05.10.2026 № 7e7a2cd217 · стр. 40 из 168

План принципиальных трасс

Силовые трассы и объёмы электромонтажа, слаботочка в объёмах · размеры в мм

Допущения и предложения на листе

Основа листа: размеры сняты с размерных цепочек растрового скана плана заказчика, на объекте не замерены; ступени наружного контура приведены к граням помещений модели (ИЗ-8, К-20, К-21); высота потолка 2700 мм принята, источника нет (К-24); тип дома и перекрытие (монолит, плита 220 мм) приняты, источника нет (К-3); толщины стен приняты (250 и 120 мм), источника нет (К-21); мощность 15 кВт принята, технических условий нет (К-25).

Знак «*» — принято, не замерено и не подтверждено (замерить на объекте): К-1, К-15: Ст К1-2, Ст В1-2; К-22: окно пом. 11 (стена В).

Знак «**» — предложение проектировщика, заказчиком не утверждено (согласовать с заказчиком): ИЗ-1, К-1: окно пом. 9 (стена В); ИЗ-5: ЩК — щит ЩРВ-П-72 вместо ЩРВ-П-54: резерв при 44 занятых модулях был меньше 20 %; ИЗ-6: дверь пом. 12 (стена Г); ИЗ-8: дверь пом. 2 (стена В) — смещение 100 → 110 мм (откос до угла был 40 мм при норме от 50 мм); ИЗ-9: ЩС — щит слаботочный: место и состав.

См. лист открытых вопросов (лист 6, записи К-1, К-3; лист 7, записи К-15, К-20–К-22, К-24, К-25; лист 9, записи ИЗ-1, ИЗ-5, ИЗ-6; лист 10, записи ИЗ-8, ИЗ-9).

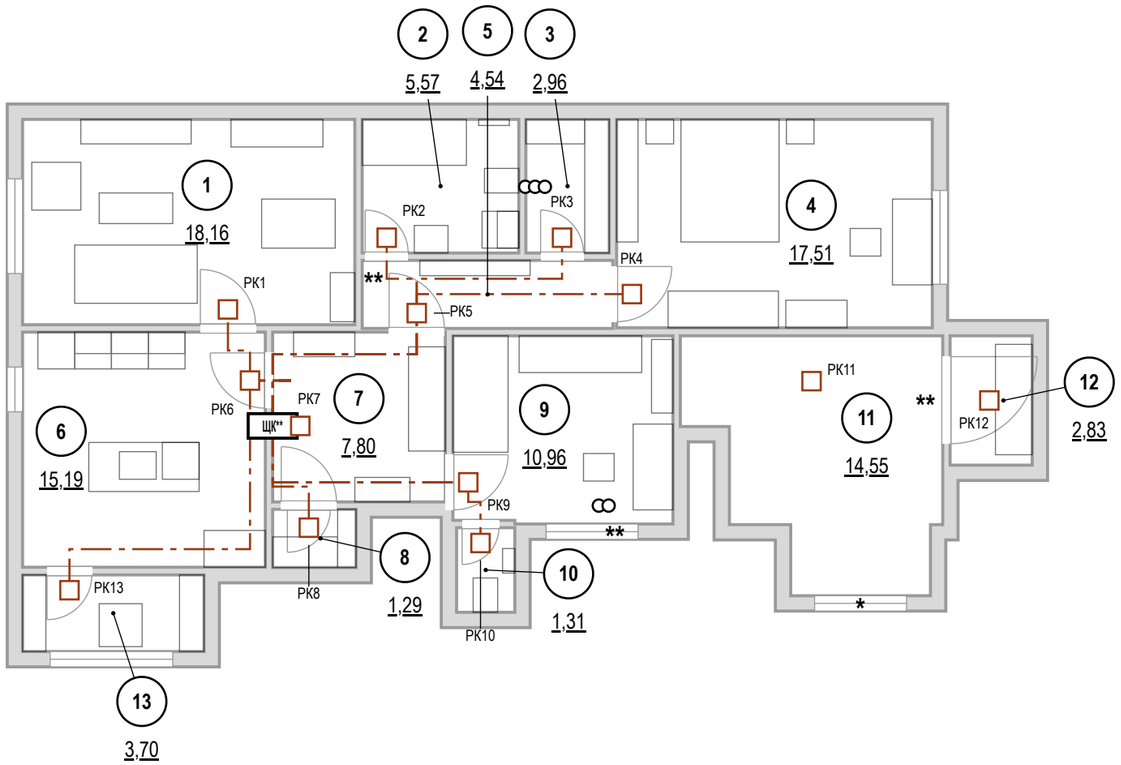

Кабель по группам ВВГнг(А)-LS, м

Гр.	мм²	Трасса	Данные
1	3×1,5	55,5	42
2	3×1,5	111,7	48
3	3×1,5	99,5	38
4	3×1,5	34,7	26
5	3×2,5	27,6	34
6	3×2,5	32,8	36
7	3×2,5	24,1	30
8	3×2,5	72,9	48
9	3×2,5	18,3	22
10	3×2,5	19,6	26

Гр.	мм²	Трасса	Данные
11	3×6	9,8	20
12	3×2,5	8,9	20
13	3×2,5	7,3	22
14	3×2,5	13,8	17
15	3×2,5	13,2	18
16	3×2,5	15,7	18
17	3×2,5	24	20
18	3×1,5	6	6
19	3×2,5	25,7	30
Σ		**621,1**	**521**

Экспликация помещений

№	Помещение	Площадь, м²
1	Зал	18,16
2	Ванная комната	5,57
3	Тёмная комната	2,96
4	Детская 1	17,51
5	Коридор	4,54
6	Кухня	15,19
7	Прихожая-коридор	7,80
8	Гардеробная 2	1,29
9	Детская 2	10,96
10	Санузел	1,31
11	Гостиная	14,55
12	Гардеробная 1	2,83
13	Балкон 1 *	3,70
	Итого (общая площадь)	102,67

Объёмы прокладки

Работа, материал	Ед.	Кол.
Гофротруба Ø20 в потолочном пространстве	м	285,8
Кабель-канал плинтуса для силовых линий	м	137
Короб или накладной канал для вертикальных спусков и подъёмов	м	101,5
Коробка распределительная (РК) над дверью помещения	шт	13
Слаботочка: Кабель коаксиальный RG-6 (75 Ом) к розеткам ТВ	м	14,5
Слаботочка: U/UTP кат. 6 (LAN, Wi-Fi, камеры)	м	70,7
Слаботочка: гофротруба Ø20 отдельно от силовых	м	76,7

Штробы — только после заключения

Работа	Ед.	Кол.
Вертикальные штробы 20×20 мм от потолка до каждой настенной точки (в маршрут без штроб не входят)	м	113,18

Условные обозначения

- ЩК — щит квартирный
- РК — распределительная коробка над дверью помещения
- магистраль от щита к РК: потолочное пространство, гофра
- мебель и сантехприборы — подложка

Примечания

1. За отметку 0,000 принят уровень чистого пола. Высоты Н — от чистого пола до оси изделия; привязки — от чистовой грани стены до оси механизма (у рамки на несколько постов — до оси рамки).
2. Розеточные и мокрые линии — через УЗО или дифавтомат с током утечки не более 30 мА (ПУЭ 7.1.79); в санузле выполнить ДСУП (ПУЭ 7.1.87–7.1.88).
3. Кабель — медный, исполнение нг(А)-LS (ГОСТ 31565-2012); скрытая прокладка только горизонтально и вертикально, фактические трассы зафиксировать исполнительной схемой до закрытия отделкой.
4. Расчёт нагрузок, токов КЗ, селективности и сечений — по проекту ЭОМ организации с допуском СРО; лист задаёт состав, расположение и группы.
5. Длины — по плану: от щита вверх в потолочное пространство, по дверям и коридору без захода в мокрые помещения к распределительной коробке над дверью, далее к точкам; вертикали считаются вниз и обратно (у последней точки цепочки — в один конец); запас 10 %. Трассы принципиальные: фактическую зафиксировать исполнительной схемой до закрытия отделкой.
6. Несущие стены не определены: штробы в стенах не выполнять. Маршрут проложен без штроб: горизонтали — за потолком в гофре (285,8 м) и в кабель-канале плинтуса (137 м), вертикали — в коробе или накладном канале (178,7 м кабеля). Точек: за потолком — 60, спуск из потолка — 11, по плинтусу — 24, плинтус и подъём — 36.
7. Вариант со штробами — работа после технического заключения: 113,18 м вертикальных штроб от потолка до каждой настенной точки; условие — только после технического заключения: стена не несущая (или вертикальная штроба в несущей согласована конструктором), глубина и ширина 20–25 мм, не в зонах 0–2 ванной. Без заключения и согласования конструктора в смету и в график эта работа не входит.
8. В данных проекта (журнал щита) длины кабеля внесены оценкой (521 м), по трассам из геометрии — 621 м (+19 %): к закупке и в смету принимать длины по трассам, а оценку в данных проекта заменить.
9. Слаботочные сети: кабели и точки считаются по лучам от ЩС** (лист слаботочных сетей): 85 м, портов патч-панели и коммутатора не менее 6; из точек 3 предложения листа слаботочки, не подтверждённые заказчиком. Изделия — в ведомости изделий.

1000 мм · печать 1:1

Изм.	Кол.уч	Лист	№ док.	Подп.	Дата
Разраб.		Кырлан А.С.			21.10.26
Пров.					
ГИП		Кырлан А.С.			21.10.26
Н. контр.					
Утв.					

ГД-2026-004-АИ

Четырёхкомнатная квартира

Общая площадь 102,67* м² · * размеры со скана, не замерены (реестр — л. 6–11, ИЗ-8, К-20, К-21)

Дизайн-проект интерьера четырёхкомнатной квартиры

Стадия	Лист	Листов
РП	36	124

План принципиальных трасс

М 1:100

Кырлан Александр Сергеевич

выпуск 05.10.2026 № 7e7a2cd217 · стр. 41 из 168

План слаботочных сетей

Интернет, ТВ, домофон · размеры в мм · высоты от чистого пола

ПРЕДВАРИТЕЛЬНО · не для производства работ · открыто пунктов: 30 (реестр — л. 6–11)

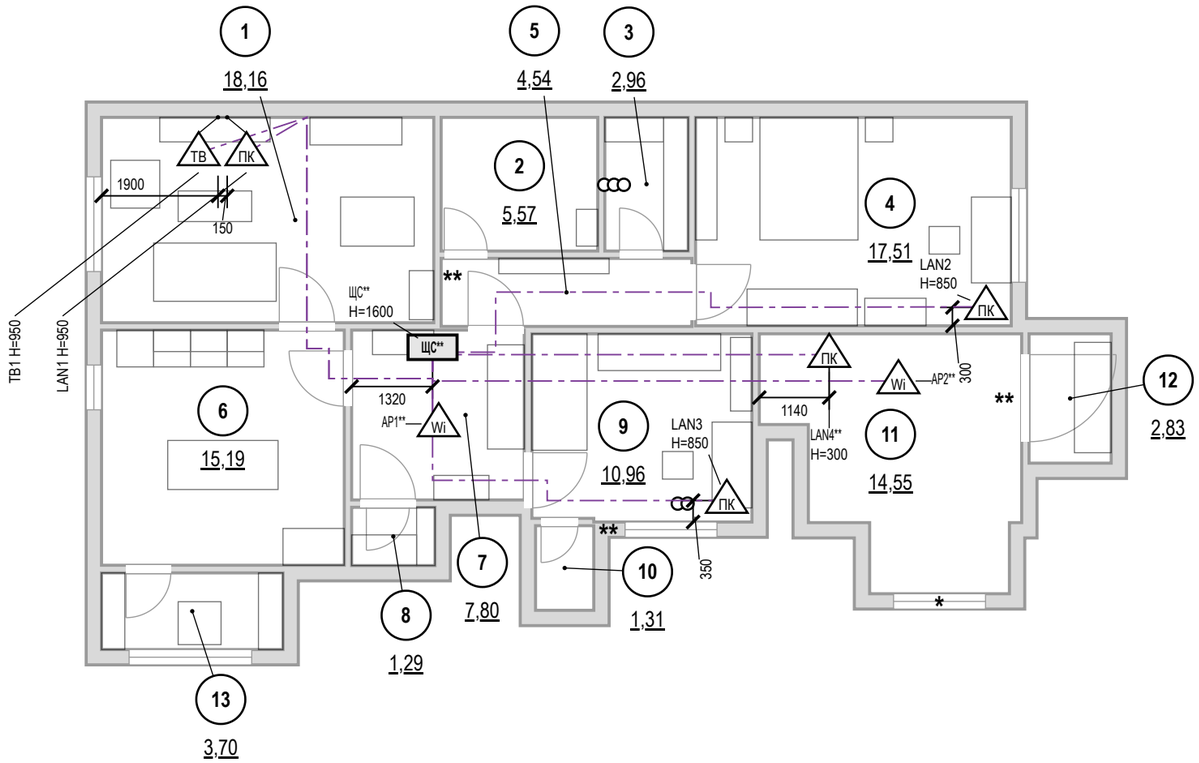

Ведомость слаботочных точек

Марка	Пом.	Назначение	H, мм	Кабель
ТВ1	1	розетка ТВ	950	коаксиальный RG-6
LAN1	1	розетка LAN (RJ45)	950	U/UTP кат. 6
LAN2	4	розетка LAN (RJ45)	850	U/UTP кат. 6
ЩС**	7	щит слаботочный	1600	ввод пров.
AP1**	7	точка доступа Wi-Fi		U/UTP кат. 6
LAN3	9	розетка LAN (RJ45)	850	U/UTP кат. 6
LAN4**	11	розетка LAN (RJ45)	300	U/UTP кат. 6
AP2**	11	точка доступа Wi-Fi		U/UTP кат. 6

Условные обозначения

- ЩС — щит слаботочный: ввод провайдера, роутер, коммутатор
- ПК — розетка компьютерная RJ45
- ТВ — розетка телевизионная
- Wi — точка доступа Wi-Fi (питание PoE)
- кабель от ЩС до точки, отдельным лучом
- мебель и сантехприборы — подложка
- (1) — номер помещения, площадь м²

Допущения и предложения на листе

Основа листа: размеры сняты с размерных цепочек растрового скана плана заказчика, на объекте не замерены; ступени наружного контура приведены к граням помещений модели (ИЗ-8, К-20, К-21); высота потолка 2700 мм принята, источника нет (К-24); тип дома и перекрытие (монолит, плита 220 мм) приняты, источника нет (К-3); толщины стен приняты (250 и 120 мм), источника нет (К-21); мощность 15 кВт принята, технических условий нет (К-25).

Знак «*» — принято, не замерено и не подтверждено (замерить на объекте): К-1, К-15: Ст К1-2, Ст В1-2; К-22: окно пом. 11 (стена В).

Знак «**» — предложение проектировщика, заказчиком не утверждено (согласовать с заказчиком): ИЗ-1, К-1: окно пом. 9 (стена В); ИЗ-6: дверь пом. 12 (стена Г); ИЗ-8: дверь пом. 2 (стена В) — смещение 100 → 110 мм (откос до угла был 40 мм при норме от 50 мм); ИЗ-9: ЩС — щит слаботочный: место и состав; AP1, AP2 — точка доступа Wi-Fi: число и места; LAN4.

См. лист открытых вопросов (лист 6, записи К-1, К-3; лист 7, записи К-15, К-20–К-22, К-24, К-25; лист 9, записи ИЗ-1, ИЗ-6; лист 10, записи ИЗ-8, ИЗ-9).

Примечания

1. За отметку 0,000 принят уровень чистого пола. Высоты H — от чистого пола до оси изделия; привязки — от чистовой грани стены до оси механизма (у рамки на несколько постов — до оси рамки).
2. Высота установки, не указанная на плане: розетки LAN и ТВ — 300 мм от чистого пола.
3. Слаботочные кабели — отдельно от силовых: в своей трубе или лотке, при параллельной прокладке не ближе 100 мм к силовым, пересечения под прямым углом; каждую точку — отдельным кабелем от ЩС** без скруток.
4. Трассы на листе — принципиальные; фактические зафиксировать исполнительной схемой до закрытия отделкой. Силовые линии, УЗО 30 мА, ДСУП, кабель нг(А)-LS — по листам розеток и щита.
5. Проект силовой части и расчёт токов КЗ — по проекту ЭОМ; слаботочная часть согласуется с провайдером и управляющей компанией (домофон, коллективное ТВ).

1000 мм · печать 1:1

Изм.	Кол.уч	Лист	№ док.	Подп.	Дата
Разраб.		Кырлан А.С.			21.10.26
Пров.					
ГИП		Кырлан А.С.			21.10.26
Н. контр.					
Утв.					

ГД-2026-004-АИ

Четырёхкомнатная квартира

Общая площадь 102,67* м² · * размеры со скана, не замерены (реестр — л. 6–11, ИЗ-8, К-20, К-21)

Дизайн-проект интерьера четырёхкомнатной квартиры

Стадия	Лист	Листов
РП	37	124

План слаботочных сетей

М 1:100

Кырлан Александр Сергеевич

выпуск 05.10.2026 № 7e7a2cd217 · стр. 42 из 168

04

Отопление и вентиляция

Кырлан Александр Сергеевич

выпуск 05.10.2026 SI 7e7a2cd217 · стр. 43 из 168

План вентиляции

Вытяжка, приток, переток · кондиционирование не предусмотрено · размеры в мм · высоты от чистого пола

ПРЕДВАРИТЕЛЬНО · не для производства работ · открыто пунктов: 30 (реестр — л. 6–11)

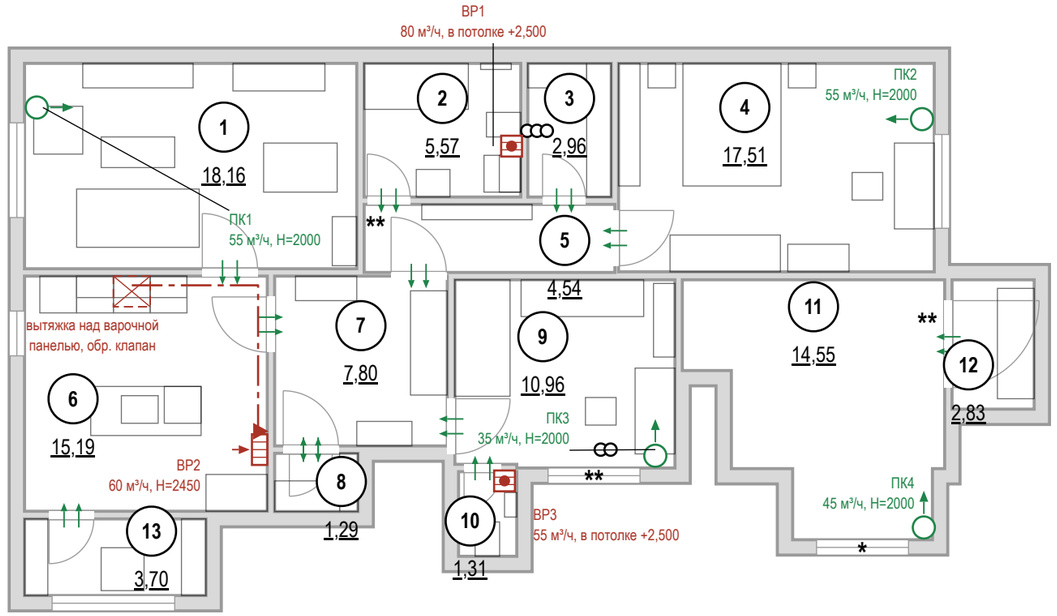

Допущения и предложения на листе

Основа листа: размеры сняты с размерных цепочек растрового скана плана заказчика, на объекте не замерены; ступени наружного контура приведены к граням помещений модели (ИЗ-8, К-20, К-21); высота потолка 2700 мм принята, источника нет (К-24); тип дома и перекрытие (монолит, плита 220 мм) приняты, источника нет (К-3); толщины стен приняты (250 и 120 мм), источника нет (К-21); мощность 15 кВт принята, технических условий нет (К-25).

Знак «*» — принято, не замерено и не подтверждено (замерить на объекте): К-1, К-15: Ст К1-2, Ст В1-2; К-22: окно пом. 11 (стена В).

Знак «**» — предложение проектировщика, заказчиком не утверждено (согласовать с заказчиком): ИЗ-1, К-1: окно пом. 9 (стена В); ИЗ-6: дверь пом. 12 (стена Г); ИЗ-8: дверь пом. 2 (стена В) — смещение 100 → 110 мм (откос до угла был 40 мм при норме от 50 мм).

См. лист открытых вопросов (лист 6, записи К-1, К-3; лист 7, записи К-15, К-20–К-22, К-24, К-25; лист 9, записи ИЗ-1, ИЗ-6; лист 10, запись ИЗ-8).

Примечания

1. Расчёт систем ОВ и подбор оборудования — проектная организация с допуском СРО; лист даёт места, трассы и привязки.
2. Нормы вытяжки — СП 54.13330.2022 (Изм. 1, 2), табл. 7.1: кухня с электроплитой 60 м³/ч, с газовой 100; ванная и совмещённый санузел 50; уборная 25; гардеробная 0,2 ч⁻¹. Приток в жилые — 3 м³/ч на 1 м² (менее 20 м² общей площади на человека), иначе 30 м³/ч на человека.
3. Венткаланы и шахты не сужать, не переносить и не закрывать; вентилятор и кухонная вытяжка — через обратный клапан, без перекрытия естественной тяги.
4. Проектные расходы — не ниже нормы, вытяжка сведена с притоком вентиляторами мокрых помещений. Клапаны — в простенке у окна, центр 2000 мм, не над кроватью, не ближе 300 мм к стоякам отопления; типоразмер — на расход.
5. Под подшивным потолком вытяжка — в потолке, воздуховодом за потолком до канала. Кухонная вытяжка в воздухообмен не включена: воздуховод не менее Ø125 в коробе, вход в канал отдельный.
6. Переток — зазор под полотнами межкомнатных дверей или переточная решётка.
7. Кондиционирование заданием не предусмотрено; при установке трассы фреона и дренажа (не менее 40 мм/м, в К1 через сифон) и питание заложить до черновых работ.
8. Привязки оборудования — по паспортам приобретённых моделей, до черновых работ.
9. Знак «*» у проёма — допущение: положение и размеры проёма не замерены (окно пом. 11, стена В); размер напечатан как принятый. Реестр: листы 6–11, вопрос К-22.
10. Клапаны ПК3, ПК4 выведены в простенок у окна, положение которого — допущение (знак «*»): после обмера окна привязку сверить.

1000 мм · печать 1:1

Условные обозначения

- стояк: К1 — канализация, В1 — ХВС, Т3 — ГВС
- 1 — номер помещения, площадь м²
- вытяжная решётка в вентканал: марка, расход м³/ч, Н центра от чистого пола
- вентилятор с обратным клапаном в подшивном потолке, воздуховод за потолком до канала
- приточный клапан (КИВ) в наружной стене: марка, расход, Н центра
- переток: зазор под полотном или переточная решётка
- кухонная вытяжка над варочной панелью
- воздуховод кухонной вытяжки в коробе под потолком
- отдельный вход воздуховода в вентканал, обратный клапан
- * — «*» принято, не замерено и не подтверждено
- ** — «**» предложение проектировщика, заказчиком не утверждено

Воздухообмен, м³/ч

№	Помещение	Выт. норма	Выт. проект	Прит. норма	Прит. проект	Устройства
1	Зал			55	55	ПК1
2	Ванная комната	50	80			ВР1
3	Тёмная комната	2				переток
4	Детская 1			53	55	ПК2
6	Кухня	60	60			ВР2
8	Гардеробная 2	1				переток
9	Детская 2			33	35	ПК3
10	Санузел	25	55			ВР3
11	Гостиная			44	45	ПК4
12	Гардеробная 1	2				переток
	Итого	**140**	**195**	**185**	**190**	

Воздухообмен квартиры — по большей из сумм притока и вытяжки: норма 185 м³/ч, проект 195 м³/ч.
Вытяжка не меньше притока — баланс сведён.

Привязки — до обмера

Венткаланы в исходных данных не заданы: решётки и вход вытяжки показаны у стояков К1 (вентблок у мокрой зоны). До черновых работ — обмер каналов и проверка тяги; лист перевыпустить по факту.

Изм.	Кол.уч	Лист	№ док.	Подп.	Дата
Разраб.		Кырлан А.С.			21.10.26
Пров.					
ГИП		Кырлан А.С.			21.10.26
Н. контр.					
Утв.					

ГД-2026-004-АИ

Четырёхкомнатная квартира

Общая площадь 102,67* м² · * размеры со скана, не замерены (реестр — л. 6–11, ИЗ-8, К-20, К-21)

Дизайн-проект интерьера четырёхкомнатной квартиры

Стадия	Лист	Листов
РП	38	124

План вентиляции

М 1:100

Кырлан Александр Сергеевич

выпуск 05.10.2026 № 7e7a2cd217 · стр. 44 из 168

План отопления

Радиаторы, стояки, подводки · размеры в мм · высоты от чистого пола

ПРЕДВАРИТЕЛЬНО · не для производства работ · открыто пунктов: 30 (реестр — л. 6–11)

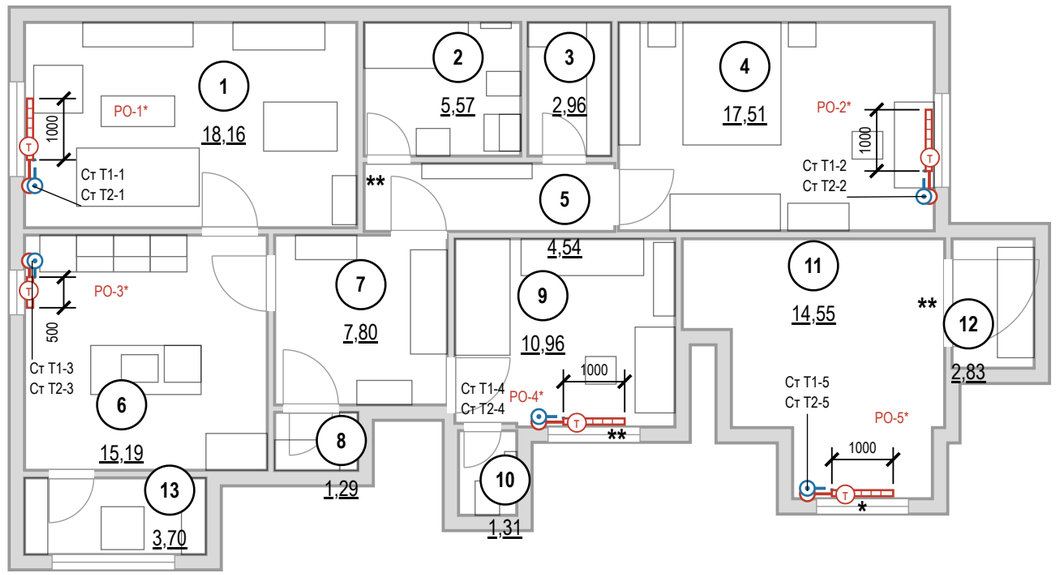

Условные обозначения

- (1) — номер помещения, площадь м²
- радиатор отопления (марка PO-N, длина по плану)
- (T) — клапан с термоголовкой на подаче
- стояк отопления, подающий (Ст Т1-N)
- стояк отопления, обратный (Ст Т2-N)
- Т1 — отопление, подающий трубопровод
- Т2 — отопление, обратный трубопровод
- * — «*» — принято, не замерено и не подтверждено
- ** — «**» — предложение проектировщика, заказчиком не утверждено

Ведомость радиаторов

Марка	Помещение	Тип	Д×В×Г, мм	Низ / стена	Q, Вт
PO-1	1. Зал	панельный*	1000×500×100	120 / 40	расч.
PO-2	4. Детская 1	панельный*	1000×500×100	120 / 40	расч.
PO-3	6. Кухня	панельный*	500×500×100	120 / 40	расч.
PO-4	9. Детская 2	панельный*	1000×500×100	120 / 40	расч.
PO-5	11. Гостиная	панельный*	1000×600×100	120 / 40	расч.

* тип и мощность — по теплотехническому расчёту
Низ — от чистого пола, стена — зазор до задней панели, мм.

Привязки — до обмера
Стояки отопления в исходных данных не заданы: показаны у откосов окон, подводки — принципиально. До черновых работ — обмер стояков и паспорта приборов; лист перевыпустить по факту.

Примечания

1. Расчёт системы отопления, теплопотерь и подбор приборов — проектная организация с допуском СРО; лист даёт места и привязки.
2. Тип, длина и мощность радиаторов — по теплотехническому расчёту; лист задаёт места, зазоры и подключение.
3. Радиаторы — под каждым окном жилых комнат и кухни, центр по оси проёма, длина 0,7 ширины окна (кратно 100); окончательно — по расчёту.
4. Зазоры радиатора: низ не менее 100 мм от чистого пола, верх не менее 100 мм до подоконника, 30–50 мм от стены до задней панели; центр по оси окна с допуском ±20 мм.
5. Радиаторы не закрывать глухими коробами и мебелью; перенос и замена приборов в многоквартирном доме — переустройство, согласование с управляющей организацией (ЖК РФ ст. 25–26); вынос на лоджию запрещён.
6. Трубы отопления через межквартирные стены не прокладывать (СП 51.13330.2011, п. 9.19); через перекрытия и перегородки — в гильзах.
7. Привязки приборов и подводок — по паспортам приобретённых радиаторов и клапанов, до черновых работ.
8. До закрытия отделкой трубопроводы отопления испытать гидростатическим давлением с оформлением акта (СП 73.13330.2016, 7.2–7.3).
9. Знак «*» у проёма — допущение: положение и размеры проёма не замерены (окно пом. 11, стена В); размер напечатан как принятый. Реестр: листы 6–11, вопрос К-22.
10. Радиаторы PO-4, PO-5 стоят по оси окна, положение которого — допущение (знак «*»): после обмера окна привязки приборов и подводок сверить.

Допущения и предложения на листе
Основа листа: размеры сняты с размерных цепочек растрового скана плана заказчика, на объекте не замерены; ступени наружного контура приведены к граням помещений модели (ИЗ-8, К-20, К-21); высота потолка 2700 мм принята, источника нет (К-24); тип дома и перекрытие (монолит, плита 220 мм) приняты, источника нет (К-3); толщины стен приняты (250 и 120 мм), источника нет (К-21); мощность 15 кВт принята, технических условий нет (К-25).
Знак «*» — принято, не замерено и не подтверждено (замерить на объекте): К-22: окно пом. 11 (стена В).
Знак «**» — предложение проектировщика, заказчиком не утверждено (согласовать с заказчиком): ИЗ-1, К-1: окно пом. 9 (стена В); ИЗ-6: дверь пом. 12 (стена Г); ИЗ-8: дверь пом. 2 (стена В) — смещение 100 → 110 мм (откос до угла был 40 мм при норме от 50 мм).
См. лист открытых вопросов (лист 6, записи К-1, К-3; лист 7, записи К-20–К-22, К-24, К-25; лист 9, записи ИЗ-1, ИЗ-6; лист 10, запись ИЗ-8).

1000 мм · печать 1:1

Изм.	Кол.уч	Лист	№ док.	Подп.	Дата
Разраб.		Кырлан А.С.			21.10.26
Пров.					
ГИП		Кырлан А.С.			21.10.26
Н. контр.					
Утв.					

ГД-2026-004-АИ

Четырёхкомнатная квартира

Общая площадь 102,67* м² · * размеры со скана, не замерены (реестр — л. 6–11, ИЗ-8, К-20, К-21)

Дизайн-проект интерьера четырёхкомнатной квартиры

Стадия	Лист	Листов
РП	39	124

План отопления

М 1:100

Кырлан Александр Сергеевич

выпуск 05.10.2026 № 7e7a2cd217 · стр. 45 из 168

05

Водоснабжение и канализация

Кырлан Александр Сергеевич

выпуск 05.10.2026 · 7e7a2cd217 · стр. 46 из 168

План выводов сантехники

Выводы В1, Т3, К1 · привязки от чистовых стен · высоты от чистого пола, мм

Фрагмент 1. Ванная комната (пом. 2)

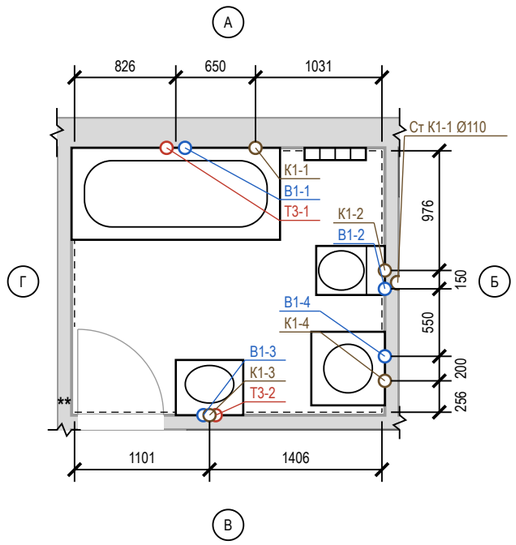

Фрагмент 2. Кухня (пом. 6)

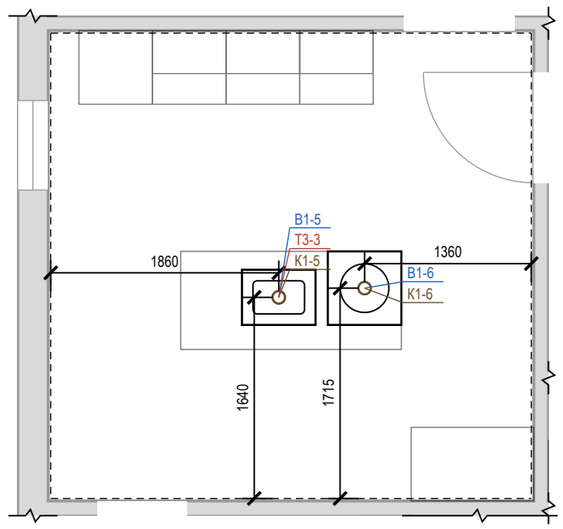

Фрагмент 3. Санузел (пом. 10)

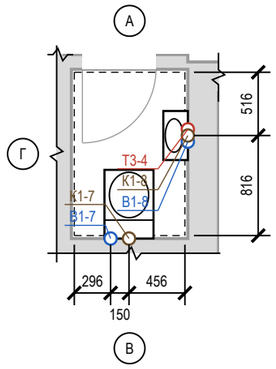

Ведомость привязок выводов

Код	Прибор	Ø	H, мм	Привязка от чист. стен, мм	Прим.
В1-1	П1 ванна	½"	800	ст. А: 901 от Г	межос. 150
Т3-1	П1 ванна	½"	800	ст. А: 751 от Г	межос. 150
К1-1	П1 ванна	Ø50	60	ст. А: 1031 от Б	
В1-2	П2 унитаз подвесной	½"	250	ст. Б: 1006 от В	в раме инсталляции
К1-2	П2 унитаз подвесной	Ø110	220	ст. Б: 976 от А	
В1-3	П3 умывальник	½"	550	ст. В: 1051 от Г	межос. 100
Т3-2	П3 умывальник	½"	550	ст. В: 1151 от Г	межос. 100
К1-3	П3 умывальник	Ø40	450	ст. В: 1101 от Г	
В1-4	П4 стиральная машина	½"	700	ст. Б: 456 от В	кран машины
К1-4	П4 стиральная машина	Ø40	700	ст. Б: 256 от В	
В1-5	П6 мойка кухонная	½"	600	1860 от Г; 1640 от В	межос. 100
Т3-3	П6 мойка кухонная	½"	600	1860 от Г; 1640 от В	межос. 100
К1-5	П6 мойка кухонная	Ø50	400	1860 от Г; 1640 от В	
В1-6	П7 посудомоечная машина	½"	550	1360 от Б; 1715 от В	кран ПММ
К1-6	П7 посудомоечная машина	Ø50	550	1360 от Б; 1715 от В	
В1-7	П8 унитаз подвесной	½"	250	ст. В: 296 от Г	в раме инсталляции
К1-7	П8 унитаз подвесной	Ø110	220	ст. В: 446 от Г	
В1-8	П9 умывальник	½"	550	ст. Б: 566 от А	межос. 100
Т3-4	П9 умывальник	½"	550	ст. Б: 466 от А	межос. 100
К1-8	П9 умывальник	Ø40	450	ст. Б: 516 от А	

* — высота по практике монтажа; сверить по паспорту прибора

Условные обозначения

- вывод В1 (код — в ведомости привязок)
- вывод Т3 (код — в ведомости привязок)
- вывод К1 (код — в ведомости привязок)
- сантехприбор по расстановке (габарит модели)
- чистовая поверхность стены (от неё привязки)
- стояк «Ст К1-N / Ст В1-N» (ГОСТ 21.601), Ø мм
- * стояк Т3 не на обмере — принят в шахте рядом со Ст В1, сверить
- линия обрыва (граница фрагмента)
- А — обозначение стены А–Г (как на развёртках)

Допущения и предложения на листе

Основа листа: размеры сняты с размерных цепочек растрового скана плана заказчика, на объекте не замерены; ступени наружного контура приведены к граням помещений модели (ИЗ-8, К-20, К-21); высота потолка 2700 мм принята, источника нет (К-24); тип дома и перекрытие (монолит, плита 220 мм) приняты, источника нет (К-3); толщины стен приняты (250 и 120 мм), источника нет (К-21); мощность 15 кВт принята, технических условий нет (К-25).

Знак «*» — принято, не замерено и не подтверждено (замерить на объекте): К-1, К-15: Ст В1-2, Ст К1-2.

Знак «**» — предложение проектировщика, заказчиком не утверждено (согласовать с заказчиком): ИЗ-8: дверь пом. 2 (стена В) — смещение 100 → 110 мм (откос до угла был 40 мм при норме от 50 мм).

Открытые вопросы и конфликты по листу: К-15, Кф-1.

См. лист открытых вопросов (лист 6, записи К-1, К-3; лист 7, записи К-15, К-20, К-21, К-24, К-25; лист 8, запись Кф-1; лист 10, запись ИЗ-8).

Примечания

1. Привязки выводов даны от чистовых поверхностей стен (облицовка на сторону: ванная комната — 24 мм (штукатурка 10 + клей 5 + плитка 9); кухня — 20 мм (по данным); санузел — 24 мм (штукатурка 10 + клей 5 + плитка 9)); эти же грани — на развёртках и в раскладке плитки. Высоты — от чистого пола помещения.
2. Высоты и межосевые, отмеченные «*», приняты по практике монтажа; до черновой разводки сверить по паспорту выбранного прибора (смеситель, инсталляция, сифон).
3. Горячая вода (Т3) — слева от холодной (В1), если смотреть на прибор. Допуск установки выводов: ±5 мм в группе, ±20 мм у отдельно стоящих.
4. Расчёт систем водоснабжения и канализации и подбор оборудования выполняет проектная организация; лист задаёт места и высоты выводов.
5. Ст Т3-2 на обмере не показаны: приняты рядом с Ст В1-2* (в МКД стоят группой); положение сверить на объекте до разметки.
6. Стояки в коробах/шахтах не замоноличивать; стояк К1 в коробе — звукоизоляция стояка в коробе без жёсткого контакта с трубой; к арматуре и ревизиям — люк не меньше 300×400.
7. Штриховая линия чистовой грани стены прерывается на длине полотна открытой двери, лежащего вдоль грани (линии не должны сливаться при печати); положение грани — по размерам, а не по штриху.

1000 мм · печать 1:1

Изм.	Кол.уч	Лист	№ док.	Подп.	Дата
Разраб.		Кырлан А.С.			21.10.26
Пров.					
ГИП		Кырлан А.С.			21.10.26
Н. контр.					
Утв.					

ГД-2026-004-АИ

Четырёхкомнатная квартира

Общая площадь 102,67* м² · * размеры со скана, не замерены (реестр — л. 6–11, ИЗ-8, К-20, К-21)

Дизайн-проект интерьера четырёхкомнатной квартиры

Стадия	Лист	Листов
РП	40	124

План выводов сантехники

М 1:50

Кырлан Александр Сергеевич

Схема разводки водопровода и канализации

Схемы систем В1, Т3, К1 · трассы принципиальные · уклоны в мм на 1 м · план М 1:400, фрагменты М 1:40

План квартиры (М 1:400)

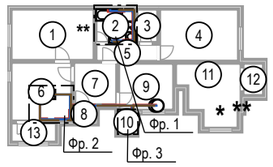

Фр. 1. Ванная комната (М 1:40)

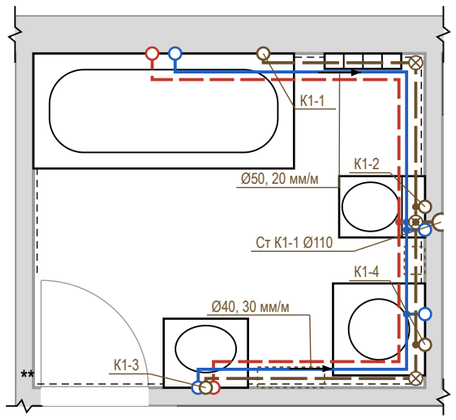

Фр. 2. Кухня (М 1:40)

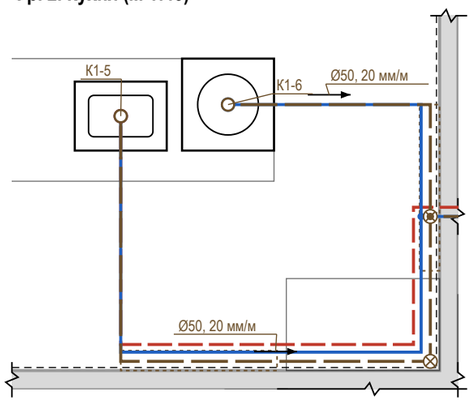

Фр. 3. Санузел (М 1:40)

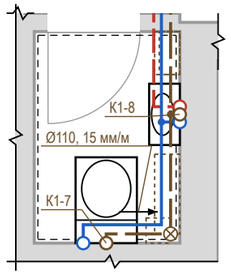

Условные обозначения

- В1 — водопровод хозяйственно-питьевой (ХВС), PP-R Ø20
- Т3 — горячее водоснабжение, подача (ГВС), PP-R Ø20
- К1 — канализация бытовая
- направление уклона К1 / пола: Ø, мм на 1 м
- ⊗ ревизия (прочистка) К1 — доступ сохранить
- • тройник (ответвление к прибору)
- короб К1 над чистым полом (ГКЛВ под плитку)
- ○ вывод В1 (код — в ведомости привязок)
- ○ вывод Т3 (код — в ведомости привязок)
- ○ вывод К1 (код — в ведомости привязок)
- сантехприбор по расстановке (габарит модели)
- ○ стояк «Ст К1-N / Ст В1-N» (ГОСТ 21.601), Ø мм
- * стояк Т3 не на обмере — принят в шахте рядом со Ст В1, сверить
- * у стояка — положение принято, не замерено, сверить
- линия обрыва (граница фрагмента)
- граница фрагмента на плане (Фр. N)

Профиль выпусков К1 (до врезки в стояк)

Выпуск	Прибор	Ø	L, м	i, мм/м	Δh, мм	Прокладка, мм
К1-7	П8 унитаз подвесной	Ø110	3,60	15	54	короб 200×140
К1-2	П2 унитаз подвесной	Ø110	0,35	20	7	над полом за приборами
К1-5	П6 мойка кухонная	Ø50	10,10	20	202	короб 290×110
К1-6	П7 посудомоечная машина	Ø50	7,60	20	152	короб 240×110
К1-1	П1 ванна	Ø50	2,30	20	46	в полу, стяжка ≥ 151
К1-3	П3 умывальник	Ø40	2,65	30	80	короб 150×110
К1-8	П9 умывальник	Ø40	2,50	30	75	короб 150×110
К1-4	П4 стиральная машина	Ø40	1,05	30	32	в полу, стяжка ≥ 127

Короб h×b: h — от чистого пола, b — от чистовой стены. Стяжка 155 мм — лист полов.

Узел ввода В1, Т3 (схема, без масштаба)

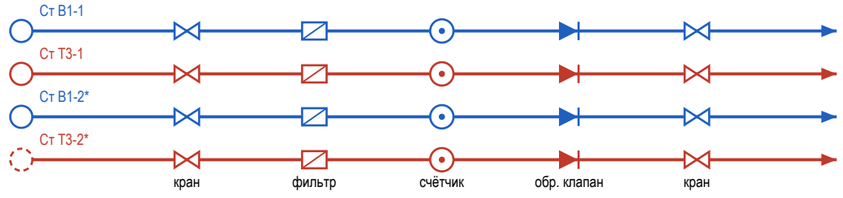

⊗ Ст К1-1, Ст К1-2*: ревизия на стояке — люк в коробе

Допущения и предложения на листе

Основа листа: размеры сняты с размерных цепочек растрового скана плана заказчика, на объекте не замерены; ступени наружного контура приведены к граням помещений модели (ИЗ-8, К-20, К-21); высота потолка 2700 мм принята, источника нет (К-24); тип дома и перекрытие (монолит, плита 220 мм) приняты, источника нет (К-3); толщины стен приняты (250 и 120 мм), источника нет (К-21); мощность 15 кВт принята, технических условий нет (К-25).

Знак «*» — принято, не замерено и не подтверждено (замерить на объекте): К-1, К-15: Ст К1-2, Ст В1-2; К-22: окно пом. 11 (стена В).

Знак «**» — предложение проектировщика, заказчиком не утверждено (согласовать с заказчиком): ИЗ-1, К-1: окно пом. 9 (стена В); ИЗ-6: дверь пом. 12 (стена Г); ИЗ-8: дверь пом. 2 (стена В) — смещение 100 → 110 мм (откос до угла был 40 мм при норме от 50 мм).

Открытые вопросы и конфликты по листу: К-15, Кф-1.

См. лист открытых вопросов (лист 6, записи К-1, К-3; лист 7, записи К-15, К-20–К-22, К-24, К-25; лист 8, запись Кф-1; лист 9, записи ИЗ-1, ИЗ-6; лист 10, запись ИЗ-8).

Примечания

1. Трассы принципиальные, построены от стояков вдоль стен помещений; фактическое положение фиксируется исполнительной схемой с привязками (фото с рулеткой) до закрытия.
2. Уклон К1 не менее 1/d и не более 150 мм/м (СП 30.13330.2020, п. 19.1), приняты практические уклоны; поворот — двумя отводами 45°, ревизия после поворота, доступ сохранить. Стояк К1 в коробе — звукоизоляция стояка в коробе, без жёсткого контакта короба с трубой.
3. Решение по К1: стяжка 155 мм не укрывает трубы (нужно Ø + Δh + 45 мм) — выпуски идут над чистым полом вдоль стен: К1-2 — за приборами и в раме инсталляции; К1-7, К1-5, К1-6, К1-3, К1-8 — в коробе ГКЛВ под плитку (размеры в профиле). Короба — на развёртках; отметку низа врезки в стояк замерить до черновых работ.
4. На каждом вводе В1 и Т3 — кран шаровой, фильтр, счётчик, обратный клапан; доступ через люк не меньше 300×400. Водопровод — в штробе стен или в коробах; трубы испытать давлением до закрытия (акт скрытых работ).
5. Расчёт систем, диаметры магистралей и подбор оборудования выполняет проектная организация; врезка и перенос стояков — по согласованию с управляющей организацией. Арматуру и привязки сверить по паспортам приборов.
6. Ст Т3-2 на обмере не показаны: приняты рядом с Ст В1-2*; положение сверить на объекте до разводки.
7. Штриховая линия чистовой грани стены прерывается на длине полотна открытой двери, лежащего вдоль грани (линии не должны сливаться при печати); положение грани — по размерам, а не по штриху.
8. Знак «*» у стояка — положение принято, не замерено (Ст К1-2*, Ст В1-2*); сверить на объекте до разметки. Реестр: листы 6–11, вопросы К-1, К-15, Кф-1.

Изм.	Кол.уч	Лист	№ док.	Подп.	Дата
Разраб.		Кырлан А.С.			21.10.26
Пров.					
ГИП		Кырлан А.С.			21.10.26
Н. контр.					
Утв.					

ГД-2026-004-АИ

Четырёхкомнатная квартира

Общая площадь 102,67* м² · * размеры со скана, не замерены (реестр — л. 6–11, ИЗ-8, К-20, К-21)

Дизайн-проект интерьера четырёхкомнатной квартиры

Стадия	Лист	Листов
РП	41	124

Схема разводки водопровода и канализации

М б/м

Кырлан Александр Сергеевич

выпуск 05.10.2026 № 7e7a2cd217 · стр. 48 из 168

Спецификация сантехнического оборудования

ПРЕДВАРИТЕЛЬНО · не для производства работ · открыто пунктов: 30 (реестр — л. 6–11)

Форма 1 ГОСТ 21.110-2013 · ГД-2026-004-АИ-ВК.СО · приборы, арматура, трубопроводы

Поз.	Наименование и техническая характеристика	Тип, марка, обозначение документа	Код продукции	Поставщик	Ед. изм.	Кол.	Масса 1 ед., кг	Примечание
	Санитарные приборы							
1	Ванна акриловая 1700×750 мм, с каркасом, экраном и отверстием слив-перелив	аналог		выбор заказчика	шт	1	35	П1
2	Унитаз подвесной безободковый, с сиденьем микролифт, крепёж и звукоизолирующая прокладка	аналог		выбор заказчика	шт	2		П2, П8
3	Инсталляция для подвесного унитаза: рама высотой 1120 мм, бачок, клавиша смыва (ось клавиши 1050 мм от чистого пола)	аналог		выбор заказчика	шт	2		П2, П8; короб ГКЛВ
4	Умывальник подвесной 550×450 мм, с отверстием под смеситель и переливом	аналог		выбор заказчика	шт	1		П3
5	Умывальник подвесной 400×200 мм, с отверстием под смеситель и переливом	аналог		выбор заказчика	шт	1		П9
6	Мойка кухонная врезная 600×450 мм, с переливом	аналог		с кухонной мебелью	шт	1		П6
7	Полотенцесушитель электрический, IP44, с терморегулятором	аналог		выбор заказчика	шт	1		П5
	Смесители, сифоны и арматура приборов							
8	Смеситель для ванны настенный однорычажный, межосевое 150 мм, с душевым набором (лейка, шланг, держатель)	аналог		выбор заказчика	шт	1		П1
9	Смеситель для умывальника однорычажный, с донным клапаном	аналог		выбор заказчика	шт	2		П3, П9
10	Смеситель кухонный однорычажный, высокий излив	аналог		выбор заказчика	шт	1		П6
11	Обвязка ванны слив-перелив Ø40/50 с сифоном	аналог		выбор заказчика	шт	1		П1
12	Сифон для умывальника бутылочный Ø32/40–50, с гофрой к выпуску	аналог		выбор заказчика	шт	2		П3, П9
13	Сифон для мойки с отводом для ПММ Ø40/50	аналог		выбор заказчика	шт	1		П6
14	Сифон для стиральной машины встраиваемый в стену Ø50, с обратным клапаном	аналог		выбор заказчика	шт	1		П4
15	Кран угловой ½"×½" с гибкой подводкой 40 см (умывальники, мойка)	аналог		выбор заказчика	шт	6		по 2 на прибор
16	Кран шаровой угловой ½"×¾" для подключения стиральной и посудомоечной машины	аналог		выбор заказчика	шт	2		П4, П7
	Трубопроводы							
17	Труба полипропиленовая PP-R PN20 Ø20×3,4 (В1)	ГОСТ 32415-2013		выбор заказчика	м	27	0,17	20,1 + 4,3 + 10 %
18	Труба PP-R, армированная стекловолокном, PN20 Ø20×2,8 (Т3)	ГОСТ 32415-2013		выбор заказчика	м	21,5	0,15	16,7 + 2,5 + 10 %
19	Труба канализационная ПП Ø40 (К1)	ГОСТ 32414-2013		выбор заказчика	м	5		2,6 + 1,6 + 10 %
20	Труба канализационная ПП Ø50 (К1)	ГОСТ 32414-2013		выбор заказчика	м	15,5		12,7 + 1,0 + 10 %
21	Труба канализационная ПП Ø110 (К1)	ГОСТ 32414-2013		выбор заказчика	м	5		3,9 + 0,4 + 10 %
	Фасонные части и выводы							
22	Отвод канализационный ПП 45° Ø40	ГОСТ 32414-2013		выбор заказчика	шт	4		2 шт. на поворот
23	Отвод канализационный ПП 45° Ø50	ГОСТ 32414-2013		выбор заказчика	шт	12		2 шт. на поворот
24	Отвод канализационный ПП 45° Ø110	ГОСТ 32414-2013		выбор заказчика	шт	10		2 шт. на поворот
25	Тройник канализационный ПП 45° (врезки ветвей)	ГОСТ 32414-2013		выбор заказчика	шт	7		
26	Ревизия канализационная ПП (после поворота трассы)	ГОСТ 32414-2013		выбор заказчика	шт	7		доступ сохранить
27	Фитинги PP-R Ø20: тройники, угольники 90° (ветви и повороты В1, Т3)	ГОСТ 32415-2013		выбор заказчика	шт	30		
28	Водорозетка PP-R Ø20×½" настенная, с креплением	ГОСТ 32415-2013		выбор заказчика	шт	12		коды — лист выводов
	Узлы ввода, люки, короба							
29	Кран шаровой латунный Ду15 PN16 (отключение ввода)	аналог		выбор заказчика	шт	4		Ст В1-1, Ст Т3-1, Ст В1-2*, Ст Т3-2*
30	Фильтр сетчатый косой Ду15	аналог		выбор заказчика	шт	4		
31	Счётчик воды крыльчатый Ду15 (ХВ, ГВ), с поверкой	аналог		выбор заказчика	шт	4		пломба УК
32	Клапан обратный Ду15	аналог		выбор заказчика	шт	4		
33	Люк ревизионный нажимной под плитку 300×400 мм	аналог		выбор заказчика	шт	4		к стоякам и арматуре
34	Звукоизоляция стояка К1 в коробе: рулонный звукоизоляционный материал ≥ 10 мм, обмотка стояка на высоту этажа	аналог		выбор заказчика	м	5,4		Ст К1-1, Ст К1-2*
35	Короб К1 над полом: профиль ПН/ПС, ГКЛВ 12,5 мм под плитку	аналог		выбор заказчика	м	6,8		сечение — лист разводки

Примечания

1. Форма 1 ГОСТ 21.110-2013, ширины граф изменены по п. 4.1. «Аналог» — аналог по характеристикам: модели внести до черновых работ, привязки выводов сверить по паспортам.
2. Бытовая техника не входит (показана арматура подключения), мойка — в комплекте кухни. Длины труб — трасса листа разводки + подъёмы + 10 %.
3. Стояк К1 в коробе — звукоизоляция стояка в коробе без жёсткого контакта короба с трубой. Стояки со «*» (Ст К1-2*, Ст В1-2*, Ст Т3-2) приняты положение и число узлов ввода сверить на объекте.
4. Расчёт систем водоснабжения и канализации, диаметры магистралей и подбор оборудования выполняет проектная организация.

Допущения и предложения на листе

Основа листа: размеры сняты с размерных цепочек растрового скана плана заказчика, на объекте не замерены; ступени наружного контура приведены к граням помещений модели (ИЗ-8, К-20, К-21); высота потолка 2700 мм принята, источника нет (К-24); тип дома и перекрытие (монолит, плита 220 мм) приняты, источника нет (К-3); толщины стен приняты (250 и 120 мм), источника нет (К-21); мощность 15 кВт принята, технических условий нет (К-25).

Знак «*» — принято, не замерено и не подтверждено (замерить на объекте): К-1, К-15: Ст К1-2, Ст В1-2.

См. лист открытых вопросов (лист 6, записи К-1, К-3; лист 7, записи К-15, К-20, К-21, К-24, К-25; лист 10, запись ИЗ-8).

Изм.	Кол.уч	Лист	№ док.	Подп.	Дата
Разраб.		Кырлан А.С.			21.10.26
Пров.					
ГИП		Кырлан А.С.			21.10.26
Н. контр.					
Утв.					

ГД-2026-004-АИ

Четырёхкомнатная квартира

Общая площадь 102,67* м² · * размеры со скана, не замерены (реестр — л. 6–11, ИЗ-8, К-20, К-21)

Дизайн-проект интерьера четырёхкомнатной квартиры

Стадия	Лист	Листов
РП	42	124

Спецификация сантехнического оборудования

М б/м

Кырлан Александр Сергеевич

выпуск 05.10.2026 № 7e7a2cd217 · стр. 49 из 168

Спецификация светильников и сценарии освещения

Светильники, ленты и блоки питания, слои света и сценарии по помещениям · б/м

Спецификация светильников

Поз.	Марки	Наименование	Установка	Кол.	P, Вт	Σ P, Вт	Ф, лм	Тц, К	Ra	Угол, °	IP	Дим.	Группа	Пом.
1	Св1–Св8, Св16–Св19, Св20**, Св21–Св24, Св25**, Св31–Св37, Св56–Св62	Встраиваемый точечный	в ГКЛ, корпус ≤ 70 мм	32	12	384	1000	3000	90	—	20	—	L1, L4, L13, L19	1, 4, 6, 11
2	Св9	Подвесной	подвес, низ H=1600	1	15	15	1200	2700	90	—	20	—	L2	1
3	Св10	Лента светодиодная 24 В	в карнизе короба, профиль с рассеивателем	5,4 м	9,6/м	52	900/м	2700	90	—	20	да	L3	1
4	Св11, Св12, Св13**, Св51	Встраиваемый точечный	в ГКЛ, корпус ≤ 70 мм	4	6	24	500	3000	90	—	44	—	L10, L12	2, 10
5	Св14, Св64**	Светильник над зеркалом, драйвер встроен	над зеркалом, H=1900, 1950	2	8	16	600	3000	90	—	44	—	L11, L12	2, 10
6	Св15, Св40–Св44, Св52, Св53, Св65**, Св66**	Встраиваемый точечный	в ГКЛ, корпус ≤ 70 мм	10	6	60	500	3000	90	—	20	—	L6, L7, L9, L16, L20	3, 7, 8, 11, 12
7	Св26, Св27, Св63**	Настенный (бра)	на стене, H=1400	3	6	18	400	2700	90	60	20	—	L14, L21	4, 9
8	Св28–Св30	Встраиваемый точечный	в ГКЛ, корпус ≤ 70 мм	3	5	15	400	3000	90	—	20	—	L8	5
9	Св38, Св39	Линейный светильник	на поверхности	1,2 м	8	16	700	3000	90	—	20	—	L5	6
10	Св45–Св50	Встраиваемый точечный	в ГКЛ, корпус ≤ 70 мм	6	13	78	1100	3000	90	—	20	—	L15	9
11	Св67**	Бра подсветки рабочего места, стол M36*	на стене, H=1300	1	7	7	450	3000	90	60	20	—	L22	9
12	Св54	Встраиваемый точечный	в ГКЛ, корпус ≤ 70 мм	1	9	9	800	3000	90	—	44	—	L17	13
		Итого		**63 шт + 6,6 м**		**694**								

LED-ленты, линейные светильники и блоки питания

Марка	Пом.	L, м	U, В	Вт/м	Σ P, Вт	БП	P БП, Вт	Загр., %	Питание	Доступ к БП
Св10	1	5,4	24	9,6	52	БП1	100	52	с одного конца	люк 300×300 в коробе потолка у стены А
Св38	6	0,6	24	—	8	БП2	30	53	встроенный ввод	в навесном модуле M26, съёмная панель
Св39	6	0,6	24	—	8	БП2	30	53	встроенный ввод	в навесном модуле M26, съёмная панель

Сценарии освещения

Пом.	Сценарий	Группы и уровни, %	Чем включается
1	Вечер	L1 общий свет (споты) — 0; L2 подвес над обеденным столом — 100; L3 лента в карнизе (диммер) — 50	S1, S2** светорегулятор
1	Гости	L1 общий свет (споты) — 100; L2 подвес над обеденным столом — 100; L3 лента в карнизе (диммер) — 100	S1, S2** светорегулятор
1	Кино	L1 общий свет (споты) — 0; L2 подвес над обеденным столом — 0; L3 лента в карнизе (диммер) — 20	S2** светорегулятор
1	Уборка	L1 общий свет (споты) — 100; L2 подвес над обеденным столом — 100; L3 лента в карнизе (диммер) — 0	S1

Слои света по помещениям

Пом.	Помещение	Слои света и группы	Тц, К	Ra	Σ P, Вт
1	Зал	общий — L1 (Св1–Св8); рабочий — L2 (Св9); акцентный — L3 (Св10)	2700 / 3000	90	163
2	Ванная комната	общий — L10 (Св11, Св12, Св13**); рабочий — L11 (Св14)	3000	90	26
3	Тёмная комната	общий — L9 (Св15)	3000	90	6
4	Детская 1	общий — L13 (Св16–Св19, Св20**, Св21–Св24, Св25**); рабочий — L14 (Св26, Св27)	2700 / 3000	90	132
5	Коридор	общий — L8 (Св28–Св30)	3000	90	15
6	Кухня	общий — L4 (Св31–Св37); рабочий — L5 (Св38, Св39)	3000	90	100
7	Прихожая-коридор	общий — L6 (Св40–Св43)	3000	90	24
8	Гардеробная 2	общий — L7 (Св44)	3000	90	6
9	Детская 2	общий — L15 (Св45–Св50); рабочий — L21 (Св63**), L22 (Св67**)	2700 / 3000	90	91
10	Санузел	общий — L12 (Св51); рабочий — L12 (Св64**)	3000	90	14
11	Гостиная	общий — L19 (Св56–Св62); акцентный — L20 (Св65**, Св66**)	3000	90	96
12	Гардеробная 1	общий — L16 (Св52, Св53)	3000	90	12
13	Балкон 1	общий — L17 (Св54)	3000	90	9

Допущения и предложения на листе

Основа листа: размеры сняты с размерных цепочек растрового скана плана заказчика, на объекте не замерены; ступени наружного контура приведены к граням помещений модели (ИЗ-8, К-20, К-21); высота потолка 2700 мм принята, источника нет (К-24); тип дома и перекрытие (монолит, плита 220 мм) приняты, источника нет (К-3); толщины стен приняты (250 и 120 мм), источника нет (К-21); мощность 15 кВт принята, технических условий нет (К-25).

Знак «*» — принято, не замерено и не подтверждено (замерить на объекте): ИЗ-1, К-13: M36 — положение и размеры стола утверждены автором (ИЗ-1); боковой свет от окна справа принят допустимым, рабочая рука того, кто сидит за столом, не известна (К-13).

Знак «**» — предложение проектировщика, заказчиком не утверждено (согласовать с заказчиком): ИЗ-2: Св63, Св67; ИЗ-3: Св64; ИЗ-4: S2 — светорегулятор добавлен под диммируемую ленту L3; уровни сценариев выбраны конвейером; ИЗ-7: Св65, Св66; ИЗ-8: Св13, Св20, Св25.

См. лист открытых вопросов (лист 6, записи К-3, К-13; лист 7, записи К-20, К-21, К-24, К-25; лист 9, записи ИЗ-1–ИЗ-4, ИЗ-7; лист 10, запись ИЗ-8).

Примечания

1. Позиции и марки Св — те же, что на плане освещения (лист 30) и в ведомости светильников (лист 32); группы L — по плану выключателей (лист 31).
2. Модели светильников не назначены: подбор по графам спецификации — поток, Тц, Ra, угол, IP и диммирование не хуже указанных, мощность не больше; встраиваемые — под глубину короба (графа «Установка»). IP 20 — сухие помещения.
3. Длина LED-ленты в карнизе — по линии карниза плана потолков (лист 44); Σ P = Вт/м × длина. Блок питания загружен не больше чем на 80 %; лента 24 В длиннее 10 м питается с двух концов; доступ к блоку питания — люк ревизии 300×300 мм или место, указанное в таблице.
4. Сценарии: уровень — доля максимальной яркости группы, %; 0 — группа выключена. Уровень ниже 100 % — только у групп на светорегуляторе (задний фронт, ТЕ) с диммируемыми драйверами и блоками питания.
5. Мощность и поток — по паспортам принятых изделий, Σ P — установленная мощность освещения. Оценка освещённости — на плане освещения; это не светотехнический расчёт.

Изм.	Кол.уч	Лист	№ док.	Подп.	Дата
Разраб.		Кырлан А.С.			21.10.26
Пров.					
ГИП		Кырлан А.С.			21.10.26
Н. контр.					
Утв.					

ГД-2026-004-АИ

Четырёхкомнатная квартира

Общая площадь 102,67* м² · * размеры со скана, не замерены (реестр — л. 6–11, ИЗ-8, К-20, К-21)

Дизайн-проект интерьера четырёхкомнатной квартиры

Стадия	Лист	Листов
РП	43	124

Спецификация светильников и сценарии освещения
М б/м

Кырлан Александр Сергеевич

выпуск 05.10.2026 № 7e7a2cd217 · стр. 50 из 168

06

Потолки и ГКЛ-конструкции

Кырлан Александр Сергеевич

выпуск 05.10.2026 · 7e7a2cd217 · стр. 51 из 168

План потолков

Уровни и марки потолков, короба с подсветкой, ниши под шторы, люки, вырезы · отметки низа от ±0,000 чистого пола · размеры в мм

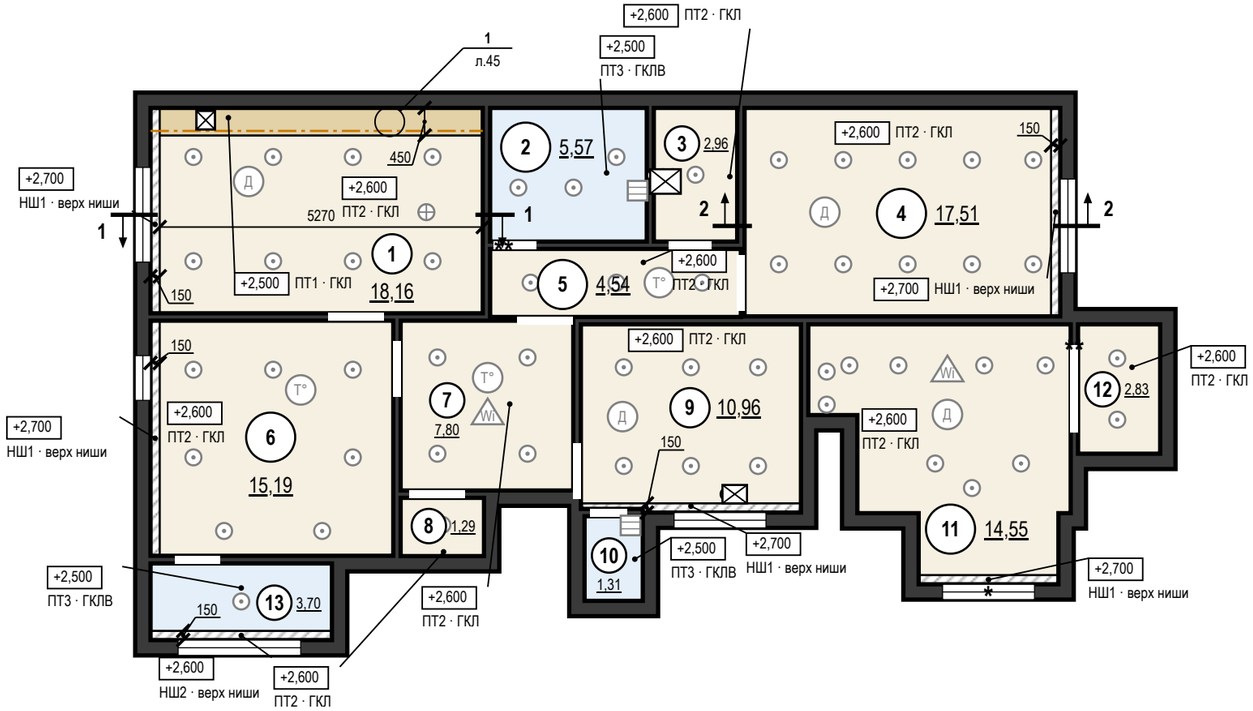

Условные обозначения

- — — ГКЛ по каркасу П113, низ +2,500, пояс-короб с карнизом LED
- ПТ1 — ГКЛ по каркасу П113, низ +2,500, пояс-короб с карнизом LED
- ПТ2 — ГКЛ по каркасу П113, низ +2,600
- ПТ3 — ГКЛВ по каркасу П113, низ +2,500
- НШ1 — ниша под шторы 150×100, верх +2,700
- НШ2 — ниша под шторы 150×100, верх +2,600
- граница уровней потолка (перепад)
- LED-лента в нише подсветки (карниз короба, ниша фигуры)
- стояк: К1 — канализация, В1 — ХВС, Т3 — ГВС
- люк ревизии в потолке 500×400, 400×300, 300×300 мм (доступ к БП LED)
- светильник встраиваемый — подложка с плана освещения
- светильник подвесной — подложка с плана освещения
- Д — извещатель дымовой на потолке — подложка
- Т° — извещатель тепловой на потолке — подложка
- Wi — точка доступа Wi-Fi на потолке — подложка
- решётка вытяжки в потолке — подложка с плана вентиляции
- линия разреза у стен помещения, стрелка — направление взгляда
- место узла: номер узла на полке, под полкой — лист
- +2,600 — отметка низа потолка, м (у ниши под шторы — верх ниши); под ней марка потолка
- 1 — номер помещения, площадь м²

Ведомость потолков

Пом.	Марка	Конструкция	Низ / верх ниши	S, м²	Q
1	ПТ1	ГКЛ П113, короб LED	+2,500	2,37	Q3
1	ПТ2	ГКЛ П113	+2,600	15,29	Q3
1	НШ1	ниша под шторы 150×100	+2,700	0,50	
2	ПТ3	ГКЛВ П113	+2,500	5,57	Q3
3	ПТ2	ГКЛ П113	+2,600	2,96	Q3
4	ПТ2	ГКЛ П113	+2,600	17,00	Q3
4	НШ1	ниша под шторы 150×100	+2,700	0,51	
5	ПТ2	ГКЛ П113	+2,600	4,54	Q3
6	ПТ2	ГКЛ П113	+2,600	14,61	Q3
6	НШ1	ниша под шторы 150×100	+2,700	0,58	
7	ПТ2	ГКЛ П113	+2,600	7,80	Q3
8	ПТ2	ГКЛ П113	+2,600	1,29	Q3
9	ПТ2	ГКЛ П113	+2,600	10,48	Q3
9	НШ1	ниша под шторы 150×100	+2,700	0,48	
10	ПТ3	ГКЛВ П113	+2,500	1,31	Q3
11	ПТ2	ГКЛ П113	+2,600	14,21	Q3
11	НШ1	ниша под шторы 150×100	+2,700	0,34	
12	ПТ2	ГКЛ П113	+2,600	2,83	Q3
13	ПТ3	ГКЛВ П113	+2,500	3,26	Q3
13	НШ2	ниша под шторы 150×100	+2,600	0,44	
		Итого		**106,37**	

Ведомость вырезов и закладных в потолке

Марка	Устройство	Кол.	Пом.
	Светильник встраиваемый (марки — план освещения)	56	1, 2, 3, 4, 5, 6, 7, 8, 9, 10, 11, 12, 13
	Светильник подвесной (марки — план освещения)	1	1
ИП1, ИП2, ИП6, ИП7	Извещатель дымовой	4	1, 4, 9, 11
ИП3**...ИП5**	Извещатель тепловой	3	5, 6, 7
АР1**, АР2**	Точка доступа Wi-Fi, PoE	2	7, 11
ВР1, ВР3	Решётка вытяжная (вентилятор)	2	2, 10
	Люк ревизии 500×400, 400×300, 300×300	4	1, 3, 9, 11

Допущения и предложения на листе

Основа листа: размеры сняты с размерных цепочек растрового скана плана заказчика, на объекте не замерены; ступени наружного контура приведены к граням помещений модели (ИЗ-8, К-20, К-21); высота потолка 2700 мм принята, источника нет (К-24); тип дома и перекрытие (монолит, плита 220 мм) приняты, источника нет (К-3); толщины стен приняты (250 и 120 мм), источника нет (К-21); мощность 15 кВт принята, технических условий нет (К-25).

Знак «*» — принято, не замерено и не подтверждено (замерить на объекте): К-1, К-15: Ст К1-2, Ст В1-2; К-22: окно пом. 11 (стена В).

Знак «**» — предложение проектировщика, заказчиком не утверждено (согласовать с заказчиком): ИЗ-1, К-1: окно пом. 9 (стена В); ИЗ-6: дверь пом. 12 (стена Г); ИЗ-8: ИП3, ИП5; дверь пом. 2 (стена В) — смещение 100 → 110 мм (откос до угла был 40 мм при норме от 50 мм); ИЗ-9: АР1, АР2 — точка доступа Wi-Fi: число и места.

См. лист открытых вопросов (лист 6, записи К-1, К-3; лист 7, записи К-15, К-20–К-22, К-24, К-25; лист 9, записи ИЗ-1, ИЗ-6; лист 10, записи ИЗ-8, ИЗ-9).

Примечания

1. За отметку ±0,000 принят уровень чистого пола сухих помещений (готовое покрытие), а не существующего пола; пол пом. 2, 10, 13 — −0,015, −0,030; верх плиты перекрытия −0,170 — расчётный по пирогу пола, не замерен; существующий пол снимается до плиты, его отметка не замерена. Отметки в прямоугольниках — низ потолка; низ плиты перекрытия +2,700, +2,600. Марка потолка — одна конструкция и отметка на весь альбом.
2. Потолки ГКЛ — каркасная система П113: подвесы через 1000 (с запасом: СП 163, табл. 14 — до 1100 при 0,15 кН/м²), несущие профили через 500, основные через 1200 мм; листы — поперёк несущих профилей. В помещениях 2, 10, 13 — ГКЛВ на оцинкованном каркасе.
3. LED-лента в алюминиевом профиле посередине карниза короба шириной 450 мм (узел 1, лист 45); длина по плану: пом. 1 — 5,4 м (в плане освещения 5,4); пом. 11 — 5,4 м.
4. Ниши под шторы 150×100 мм — на всю длину стены с окном; карниз — на закладной до обшивки (узел 2, лист 45).
5. Примыкание к стенам: теневой шов 15 мм, техзазор 3 мм — пом. 1, 11, по стенам, выровненным штукатуркой (узел 1); пом. 2, 3, 4, 5, 6, 7, 8, 9, 10, 12, 13 — разделительная лента.
6. Светильники и потолочные устройства — подложка с планов освещения, слаботочных систем и вентиляции (положение — по ним); вырезы и закладные — по ведомости на листе, до обшивки; отверстия не совмещать с профилями, глубина корпуса светильника до 70 мм.
7. Разрезы 1–1, 2–2 — на листе 45; высоты мебели и дверных блоков сверены с низом потолка в разрезах.
8. Узлы по выноскам на плане: узлы 1, 2 — лист 45.
9. Шпаклевание ГКЛ и условия приёмки — Q3: рассеянный дневной свет, осмотр с 2 м; боковой свет не оценивается.
10. Люки ревизии 500×400, 400×300, 300×300 мм — по центру блоков питания LED (ревизия, ревизия, блок питания LED БП1, блок питания LED БП1; координаты — план освещения).

1000 мм · печать 1:1

Изм.	Кол.уч	Лист	№ док.	Подп.	Дата
Разраб.		Кырлан А.С.			21.10.26
Пров.					
ГИП		Кырлан А.С.			21.10.26
Н. контр.					
Утв.					

ГД-2026-004-АИ

Четырёхкомнатная квартира

Общая площадь 102,67* м² · * размеры со скана, не замерены (реестр — л. 6–11, ИЗ-8, К-20, К-21)

Дизайн-проект интерьера четырёхкомнатной квартиры

Стадия	Лист	Листов
РП	44	124

План потолков

М 1:100

Кырлан Александр Сергеевич

выпуск 05.10.2026 № 7e7a2cd217 · стр. 52 из 168

Разрезы и узлы потолков

Разрезы по потолкам с отметками уровней · узлы коробов и ниш · размеры в мм

Разрез 1–1 (М 1:40)

Пом. 1 Зал; линия разреза — план потолков, лист 44

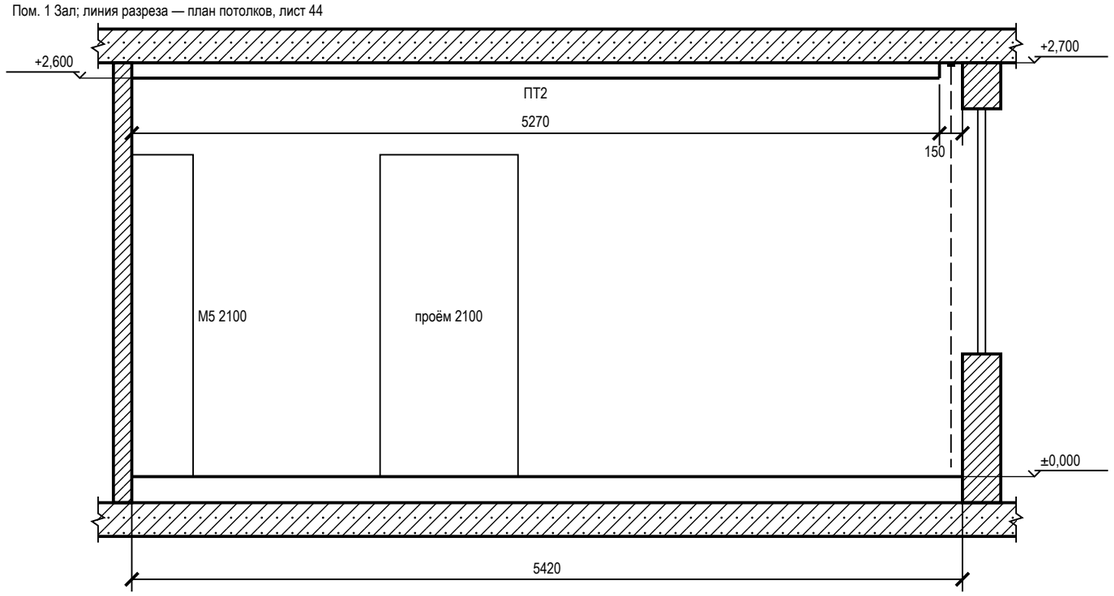

Разрез 2–2 (М 1:40)

Пом. 4 Детская 1; линия разреза — план потолков, лист 44

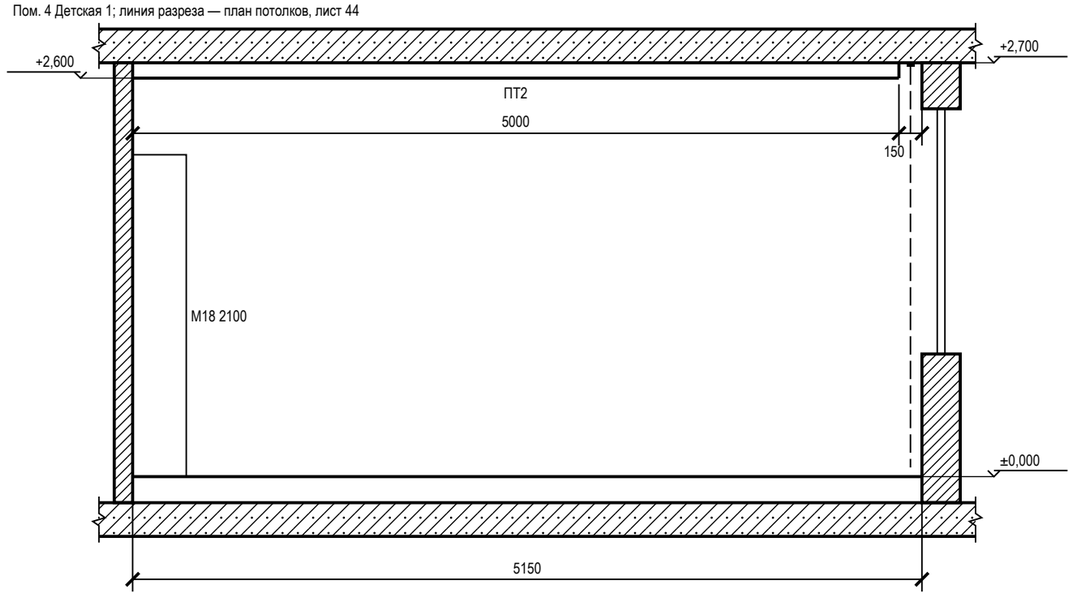

1 Короб с LED-подсветкой, теневой шов (М 1:10)

Пом. 1, 11; карниз 150×100, щель под свет 60 мм

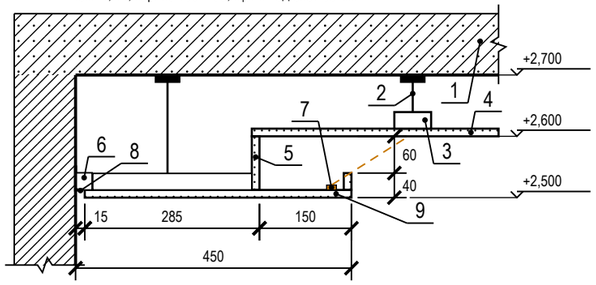

1 — плита перекрытия
2 — подвес прямой, шаг 1000 мм
3 — ПП 60×27: несущие через 500, основные через 1200 мм
4 — ГКЛ 12,5 по П113 — верхний уровень
5 — задняя стенка и бортик карниза — ГКЛ 12,5
6 — ПН 28×27 по периметру, к стене через 500 мм
7 — LED-лента в алюминиевом профиле
8 — теневой профиль: шов 15 мм, зазор 3 мм
9 — низ короба — ГКЛ 12,5 по ПП 60×27

2 Ниша под шторы (М 1:10)

Пом. 1, 4, 6, 9, 11, 13; без подсветки; закладные под карниз — до обшивки

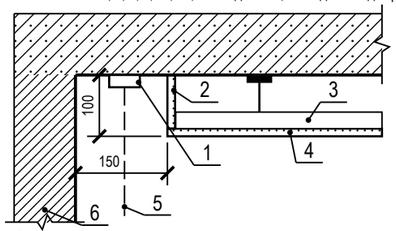

1 — карниз (шина), высота с верхом портьеры 80 мм
2 — стенка ниши — ГКЛ 12,5
3 — ПП 60×27 — каркас короба
4 — низ короба нижнего уровня — ГКЛ 12,5
5 — портьера
6 — стена с окном

Отметки по помещениям, м

Пом.	низ потолка	верх ниши	низ плиты
1, 4, 6, 9, 11	+2,600	+2,700	+2,700
13	+2,500	+2,600	+2,600

Условные обозначения

- плита перекрытия в сечении
- стена в сечении
- потолок ГКЛ в сечении; под линией — марка потолка (план потолков)
- мебель и дверные проёмы за секущей плоскостью; число — марка и верх от чистого пола, мм
- портьера в нише под шторы

Допущения и предложения на листе

Основа листа: размеры сняты с размерных цепочек растрового скана плана заказчика, на объекте не замерены; ступени наружного контура приведены к граням помещений модели (ИЗ-8, К-20, К-21); высота потолка 2700 мм принята, источника нет (К-24); тип дома и перекрытие (монолит, плита 220 мм) приняты, источника нет (К-3); толщины стен приняты (250 и 120 мм), источника нет (К-21); мощность 15 кВт принята, технических условий нет (К-25).
См. лист открытых вопросов (лист 6, запись К-3; лист 7, записи К-20, К-21, К-24, К-25; лист 10, запись ИЗ-8).

Примечания

1. Разрезы — по линиям 1–1, 2–2 на плане потолков (лист 44). Отметки — от ±0,000 чистого пола, м; размеры — мм.
2. Высоты мебели и дверных блоков за секущей плоскостью сверены с низом потолка над ними: верх ниже низа короба и поля.
3. ГКЛ 12,5 мм по каркасу П113; перепад уровней и бортик карниза — ГКЛ по ПП 60×27 (узел 1 — на этом листе). Ниша под шторы — на всю длину стены с окном, карниз на закладной до обшивки (узел 2 — на этом листе).
4. Толщины плит перекрытия и пирога пола показаны условно.
5. Сечения потолков по помещениям М 1:10 (отметки помещения, профили, подвесы, крепёж, изделия) — листы 47–48.
6. Ведомость объёмов потолков (лист ГКЛ, профиль, подвесы, лента, блоки питания, люки) — на листе 46.

1000 мм · печать 1:1

Изм.	Кол.уч	Лист	№ док.	Подп.	Дата
Разраб.		Кырлан А.С.			21.10.26
Пров.					
ГИП		Кырлан А.С.			21.10.26
Н. контр.					
Утв.					

ГД-2026-004-АИ

Четырёхкомнатная квартира

Общая площадь 102,67* м² · * размеры со скана, не замерены (реестр — л. 6–11, ИЗ-8, К-20, К-21)

Дизайн-проект интерьера четырёхкомнатной квартиры

Стадия	Лист	Листов
РП	45	124

Разрезы и узлы потолков

М 1:40; 1:10

Кырлан Александр Сергеевич

выпуск 05.10.2026 № 7e7a2cd217 · стр. 53 из 168

Разрезы и узлы потолков (продолжение)

Ведомость объёмов · размеры в мм

Ведомость объёмов потолков

Позиция	Ед.	Кол.	Пом.
Лист ГКЛ 12,5	м²	98,99	1, 3, 4, 5, 6, 7, 8, 9, 11, 12
Лист ГКЛВ 12,5	м²	10,88	2, 10, 13
Борта и карнизы (входят в площади листов выше)	м²	3,50	1, 4, 6, 9, 11, 13
Профиль ПП 60×27	м	307,26	1, 2, 3, 4, 5, 6, 7, 8, 9, 10, 11, 12, 13
Профиль ПН 28×27	м	198,10	1, 2, 3, 4, 5, 6, 7, 8, 9, 10, 11, 12, 13
Подвес прямой	шт.	102	1, 2, 3, 4, 5, 6, 7, 8, 9, 10, 11, 12, 13
Анкер-клин к плите	шт.	102	1, 2, 3, 4, 5, 6, 7, 8, 9, 10, 11, 12, 13
Шуруп TN 3,5×25	шт.	2527	1, 2, 3, 4, 5, 6, 7, 8, 9, 10, 11, 12, 13
Лента армирующая для швов	м	131,84	1, 2, 3, 4, 5, 6, 7, 8, 9, 10, 11, 12, 13
Шпаклёвка для швов	кг	43,95	1, 2, 3, 4, 5, 6, 7, 8, 9, 10, 11, 12, 13
Грунтовка (швы)	л	10,99	1, 2, 3, 4, 5, 6, 7, 8, 9, 10, 11, 12, 13
Лента разделительная по периметру	м	143,31	1, 2, 3, 4, 5, 6, 7, 8, 9, 10, 11, 12, 13
Сплошная шпаклёвка и окраска (площадь развёртки)	м²	109,87	1, 2, 3, 4, 5, 6, 7, 8, 9, 10, 11, 12, 13
Лента LED	м	5,42	1
Требуемая мощность блоков питания	Вт	68	1
Установленная мощность блоков питания	Вт	100	1
Блок питания LED	шт.	1	1
Люк ревизии	шт.	4	1, 3, 9, 11

Допущения и предложения на листе

Основа листа: размеры сняты с размерных цепочек растрового скана плана заказчика, на объекте не замерены; ступени наружного контура приведены к граням помещений модели (ИЗ-8, К-20, К-21); высота потолка 2700 мм принята, источника нет (К-24); тип дома и перекрытие (монолит, плита 220 мм) приняты, источника нет (К-3); толщины стен приняты (250 и 120 мм), источника нет (К-21); мощность 15 кВт принята, технических условий нет (К-25).

См. лист открытых вопросов (лист 6, запись К-3; лист 7, записи К-20, К-21, К-24, К-25; лист 10, запись ИЗ-8).

Примечания

1. ГКЛ 12,5 мм по каркасу П113; узлы коробов и ниш под шторы: узел 1 — лист 45; узел 2 — лист 45; условные обозначения разрезов — на листе 45.
2. Ведомость объёмов — по геометрии плана потолков: Лист ГКЛ 12,5 — плоскости уровней + борта (без арочных участков); Лист ГКЛВ 12,5 — плоскости уровней + борта; Борта и карнизы — длина перепада × перепад; Профиль ПП 60×27 — S × (1/шаг несущ. + 1/шаг осн.) + стойки бортов; Профиль ПН 28×27 — периметр стен + 2 × перепады + карнизы; Подвес прямой — по раскладке: S уровня / (шаг осн. × шаг подвесов), пояс уже шага — ряд вдоль пояса, фигура — по контуру; шаг подвесов — не больше табл. 14 СП 163; Анкер-клин к плите — по одному на подвес (Knauf П113); Шуруп TN 3,5×25 — 23 шт./м² (Knauf П113, табл. 2 альбома П 11); Лента армирующая для швов — 1,2 м/м² листа (Knauf); Шпаклёвка для швов — 0,4 кг/м² листа, только швы (Knauf); Грунтовка (швы) — 0,1 л/м² листа, только швы (Knauf); Лента разделительная по периметру — периметр стен под потолком ГКЛ; Сплошная шпаклёвка и окраска (площадь развёртки) — плоскости + борта; расход — по паспорту материала (норма на сплошной слой не подтверждена, knowledge/ceilings.md 2.3); Лента LED — по оси карниза и ниши фигуры (план потолков); Требуемая мощность блоков питания — Вт/м × длина × 1,3; Установленная мощность блоков питания — сумма мощностей блоков по плану освещения; Блок питания LED — блоки потолочных лент по плану освещения (БП1); Люк ревизии — план потолков; без запаса на подрезку (при закупке листа: ×1,075 при S > 20 м², ×1,175 — 10–20 м², ×1,275 — < 10 м²).

Изм.	Кол.уч	Лист	№ док.	Подп.	Дата
Разраб.		Кырлан А.С.			21.10.26
Пров.					
ГИП		Кырлан А.С.			21.10.26
Н. контр.					
Утв.					

ГД-2026-004-АИ

Четырёхкомнатная квартира

Общая площадь 102,67* м² · * размеры со скана, не замерены (реестр — л. 6–11, ИЗ-8, К-20, К-21)

Дизайн-проект интерьера четырёхкомнатной квартиры

Стадия	Лист	Листов
РП	46	124

Разрезы и узлы потолков (продолжение)

М б/м

Кырлан Александр Сергеевич

выпуск 05.10.2026 № 7e7a2cd217 · стр. 54 из 168

Разрезы и узлы потолков (продолжение)

Сечения потолков М 1:10 · пом. 1, 4, 6, 9, 11 · профили, подвесы, крепёж, изделия · размеры в мм

Сечение 1.1. Короб с LED-подсветкой, теневой шов (М 1:10)

Пом. 1 Зал; карниз 150×100, щель под свет 60 мм

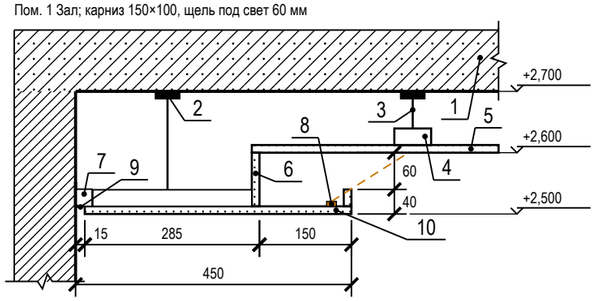

1 — плита перекрытия
2 — анкер-клин к плите — по одному на подвес
3 — подвес прямой, шаг 1000 мм
4 — ПП 60×27: несущие через 500, основные через 1200 мм; соединители одноуровневые, шурупы LN 3,5×9
5 — ГКЛ 12,5 по П113 — верхний уровень; шурупы TN 3,5×25 через 170 мм
6 — задняя стенка и бортик карниза — ГКЛ 12,5
7 — ПН 28×27 по периметру — дюбель-гвоздь через ≤ 500 мм, не менее 3 на профиль
8 — LED-лента 9,6 Вт/м, 24 В в алюминиевом профиле
9 — теневой профиль: шов 15 мм, зазор 3 мм
10 — низ короба — ГКЛ 12,5 по ПП 60×27

Сечение 1.2. Ниша под шторы (М 1:10)

Пом. 1 Зал; без подсветки; закладные под карниз — до обшивки

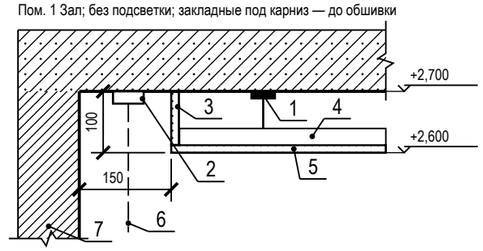

1 — анкер-клин к плите — по одному на подвес; подвес прямой, шаг 1000 мм
2 — карниз (шина), высота с верхом портьеры 80 мм
3 — стенка ниши — ГКЛ 12,5
4 — ПП 60×27 — каркас короба, основные через 1200 мм; соединители одноуровневые, шурупы LN 3,5×9
5 — низ короба нижнего уровня — ГКЛ 12,5; шурупы TN 3,5×25 через 170 мм
6 — портьера
7 — стена с окном

Сечение 1.3. Примыкание потолка к стене (М 1:10)

Пом. 1 Зал; примыкание — разделительная лента

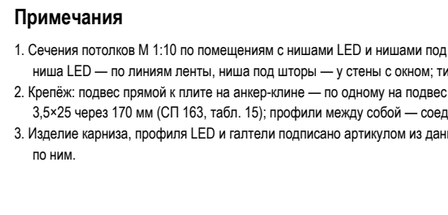

1 — плита перекрытия
2 — анкер-клин к плите — по одному на подвес
3 — подвес прямой, шаг 1000 мм
4 — ПН 28×27 по периметру — дюбель-гвоздь через ≤ 500 мм, не менее 3 на профиль
5 — ПП 60×27 несущий (вид) через 500 мм, в ПН
6 — ПП 60×27 основной (сечение) через 1200 мм; соединители одноуровневые, шурупы LN 3,5×9
7 — лента разделительная по стене, шов зашпаклёван
8 — ГКЛ 12,5 по П113; шурупы TN 3,5×25 через 170 мм

Сечение 4.1. Ниша под шторы (М 1:10)

Пом. 4 Детская 1, 6 Кухня, 9 Детская 2; без подсветки; закладные под карниз — до обшивки

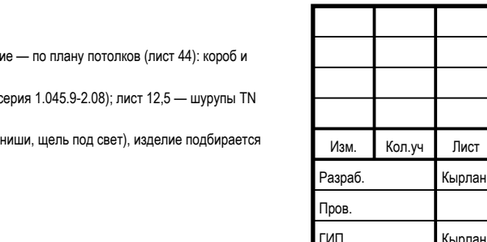

1 — анкер-клин к плите — по одному на подвес; подвес прямой, шаг 1000 мм
2 — карниз (шина), высота с верхом портьеры 80 мм
3 — стенка ниши — ГКЛ 12,5
4 — ПП 60×27 — каркас короба, основные через 1200 мм; соединители одноуровневые, шурупы LN 3,5×9
5 — низ короба нижнего уровня — ГКЛ 12,5; шурупы TN 3,5×25 через 170 мм
6 — портьера
7 — стена с окном

Сечение 4.2. Примыкание потолка к стене (М 1:10)

Пом. 4 Детская 1, 6 Кухня, 9 Детская 2; примыкание — разделительная лента

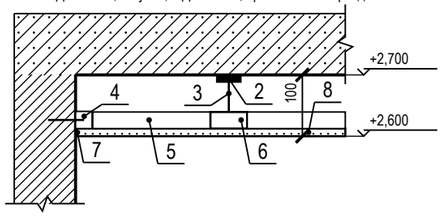

1 — плита перекрытия
2 — анкер-клин к плите — по одному на подвес
3 — подвес прямой, шаг 1000 мм
4 — ПН 28×27 по периметру — дюбель-гвоздь через ≤ 500 мм, не менее 3 на профиль
5 — ПП 60×27 несущий (вид) через 500 мм, в ПН
6 — ПП 60×27 основной (сечение) через 1200 мм; соединители одноуровневые, шурупы LN 3,5×9
7 — лента разделительная по стене, шов зашпаклёван
8 — ГКЛ 12,5 по П113; шурупы TN 3,5×25 через 170 мм

Сечение 11.1. Короб с LED-подсветкой, теневой шов (М 1:10)

Пом. 11 Гостиная; карниз 150×100, щель под свет 60 мм

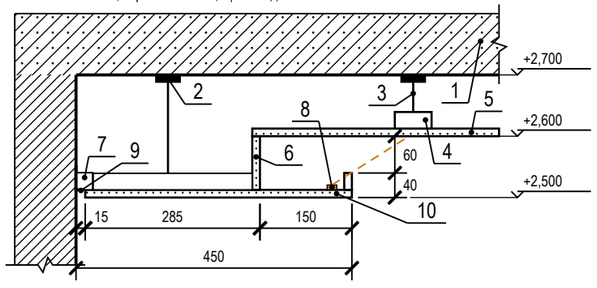

1 — плита перекрытия
2 — анкер-клин к плите — по одному на подвес
3 — подвес прямой, шаг 1000 мм
4 — ПП 60×27: несущие через 500, основные через 1200 мм; соединители одноуровневые, шурупы LN 3,5×9
5 — ГКЛ 12,5 по П113 — верхний уровень; шурупы TN 3,5×25 через 170 мм
6 — задняя стенка и бортик карниза — ГКЛ 12,5
7 — ПН 28×27 по периметру — дюбель-гвоздь через ≤ 500 мм, не менее 3 на профиль
8 — LED-лента в алюминиевом профиле
9 — теневой профиль: шов 15 мм, зазор 3 мм
10 — низ короба — ГКЛ 12,5 по ПП 60×27

Условные обозначения

— · — LED-лента в нише подсветки (карниз короба, ниша фигуры)

Допущения и предложения на листе

Основа листа: размеры сняты с размерных цепочек растрового скана плана заказчика, на объекте не замерены; ступени наружного контура приведены к граням помещений модели (ИЗ-8, К-20, К-21); высота потолка 2700 мм принята, источника нет (К-24); тип дома и перекрытие (монолит, плита 220 мм) приняты, источника нет (К-3); толщины стен приняты (250 и 120 мм), источника нет (К-21); мощность 15 кВт принята, технических условий нет (К-25).

См. лист открытых вопросов (лист 6, запись К-3; лист 7, записи К-20, К-21, К-24, К-25; лист 10, запись ИЗ-8).

Примечания

1. Сечения потолков М 1:10 по помещениям с нишами LED и нишами под шторы: отметки и размеры этого помещения от ±0,000 чистого пола (м, мм). Положение — по плану потолков (лист 44): короб и ниша LED — по линиям ленты, ниша под шторы — у стены с окном; типовые узлы по группам помещений — на листе 45.
2. Крепёж: подвес прямой к плите на анкер-клине — по одному на подвес (Knauf П113); ПН к стенам — дюбель-гвоздь через ≤ 500 мм, не менее 3 на профиль (серия 1.045.9-2.08); лист 12,5 — шурупы TN 3,5×25 через 170 мм (СП 163, табл. 15); профили между собой — соединители одноуровневые, шурупы LN 3,5×9.
3. Изделие карниза, профиля LED и галтели подписано артикулом из данных; где артикул не выбран, сечение дано по габаритам из данных (ширина и глубина ниши, щель под свет), изделие подбирается по ним.

1000 мм · печать 1:1

Изм.	Кол.уч	Лист	№ док.	Подп.	Дата
Разраб.		Кырлан А.С.			21.10.26
Пров.					
ГИП		Кырлан А.С.			21.10.26
Н. контр.					
Утв.					

ГД-2026-004-АИ

Четырёхкомнатная квартира

Общая площадь 102,67* м² · * размеры со скана, не замерены (реестр — л. 6–11, ИЗ-8, К-20, К-21)

Дизайн-проект интерьера четырёхкомнатной квартиры

Стадия	Лист	Листов
РП	47	124

Разрезы и узлы потолков (продолжение)

М 1:10

Кырлан Александр Сергеевич

выпуск 05.10.2026 № 7e7a2cd217 · стр. 55 из 168

Разрезы и узлы потолков (продолжение)

Сечения потолков М 1:10 · пом. 11, 13 · профили, подвесы, крепёж, изделия · размеры в мм

Сечение 11.2. Ниша под шторы (М 1:10)

Пом. 11 Гостиная; без подсветки; закладные под карниз — до обшивки

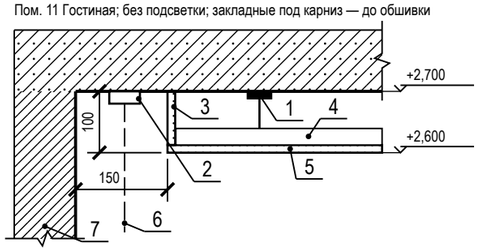

1 — анкер-клин к плите — по одному на подвес; подвес прямой, шаг 1000 мм
2 — карниз (шина), высота с верхом портьеры 80 мм
3 — стенка ниши — ГКЛ 12,5
4 — ПП 60×27 — каркас короба, основные через 1200 мм; соединители одноуровневые, шурупы LN 3,5×9
5 — низ короба нижнего уровня — ГКЛ 12,5; шурупы TN 3,5×25 через 170 мм
6 — портьера
7 — стена с окном

Сечение 11.3. Примыкание потолка к стене (М 1:10)

Пом. 11 Гостиная; примыкание — разделительная лента

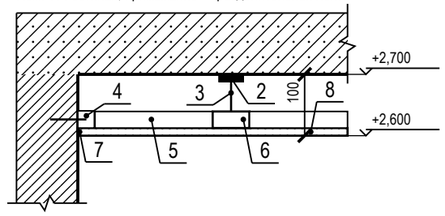

1 — плита перекрытия
2 — анкер-клин к плите — по одному на подвес
3 — подвес прямой, шаг 1000 мм
4 — ПН 28×27 по периметру — дюбель-гвоздь через ≤ 500 мм, не менее 3 на профиль
5 — ПП 60×27 несущий (вид) через 500 мм, в ПН
6 — ПП 60×27 основной (сечение) через 1200 мм; соединители одноуровневые, шурупы LN 3,5×9
7 — лента разделительная по стене, шов зашпаклёван
8 — ГКЛ 12,5 по П113; шурупы TN 3,5×25 через 170 мм

Сечение 13.1. Ниша под шторы (М 1:10)

Пом. 13 Балкон 1; без подсветки; закладные под карниз — до обшивки

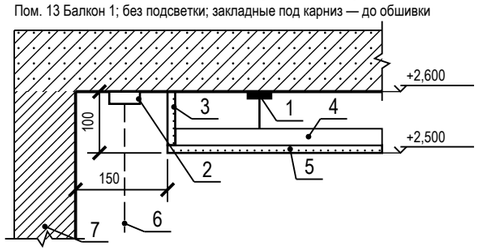

1 — анкер-клин к плите — по одному на подвес; подвес прямой, шаг 1000 мм
2 — карниз (шина), высота с верхом портьеры 80 мм
3 — стенка ниши — ГКЛВ 12,5
4 — ПП 60×27 — каркас короба, основные через 1200 мм; соединители одноуровневые, шурупы LN 3,5×9
5 — низ короба нижнего уровня — ГКЛВ 12,5; шурупы TN 3,5×25 через 170 мм
6 — портьера
7 — стена с окном

Сечение 13.2. Примыкание потолка к стене (М 1:10)

Пом. 13 Балкон 1; примыкание — разделительная лента

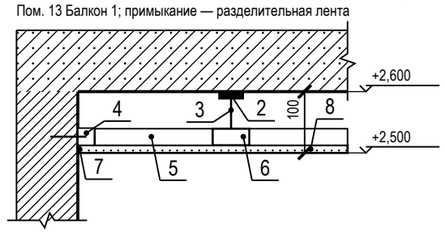

1 — плита перекрытия
2 — анкер-клин к плите — по одному на подвес
3 — подвес прямой, шаг 1000 мм
4 — ПН 28×27 по периметру — дюбель-гвоздь через ≤ 500 мм, не менее 3 на профиль
5 — ПП 60×27 несущий (вид) через 500 мм, в ПН
6 — ПП 60×27 основной (сечение) через 1200 мм; соединители одноуровневые, шурупы LN 3,5×9
7 — лента разделительная по стене, шов зашпаклёван
8 — ГКЛВ 12,5 по П113; шурупы TN 3,5×25 через 170 мм

Допущения и предложения на листе

Основа листа: размеры сняты с размерных цепочек растрового скана плана заказчика, на объекте не замерены; ступени наружного контура приведены к граням помещений модели (ИЗ-8, К-20, К-21); высота потолка 2700 мм принята, источника нет (К-24); тип дома и перекрытие (монолит, плита 220 мм) приняты, источника нет (К-3); толщины стен приняты (250 и 120 мм), источника нет (К-21); мощность 15 кВт принята, технических условий нет (К-25).
См. лист открытых вопросов (лист 6, запись К-3; лист 7, записи К-20, К-21, К-24, К-25; лист 10, запись ИЗ-8).

Примечания

1. Сечения потолков М 1:10 по помещениям с нишами LED и нишами под шторы: отметки и размеры этого помещения от ±0,000 чистого пола (м, мм). Положение — по плану потолков (лист 44): короб и ниша LED — по линиям ленты, ниша под шторы — у стены с окном; типовые узлы по группам помещений — на листе 45.
2. Крепёж: подвес прямой к плите на анкер-клине — по одному на подвес (Knauf П113); ПН к стенам — дюбель-гвоздь через ≤ 500 мм, не менее 3 на профиль (серия 1.045.9-2.08); лист 12,5 — шурупы TN 3,5×25 через 170 мм (СП 163, табл. 15); профили между собой — соединители одноуровневые, шурупы LN 3,5×9.
3. Изделие карниза, профиля LED и галтели подписано артикулом из данных; где артикул не выбран, сечение дано по габаритам из данных (ширина и глубина ниши, щель под свет), изделие подбирается по ним.

1000 мм · печать 1:1

Изм.	Кол.уч	Лист	№ док.	Подп.	Дата
Разраб.		Кырлан А.С.			21.10.26
Пров.					
ГИП		Кырлан А.С.			21.10.26
Н. контр.					
Утв.					

ГД-2026-004-АИ

Четырёхкомнатная квартира

Общая площадь 102,67* м² · * размеры со скана, не замерены (реестр — л. 6–11, ИЗ-8, К-20, К-21)

Дизайн-проект интерьера четырёхкомнатной квартиры

Стадия	Лист	Листов
РП	48	124

Разрезы и узлы потолков (продолжение)

М 1:10

Кырлан Александр Сергеевич

выпуск 05.10.2026 № 7e7a2cd217 · стр. 56 из 168

Раскладка плитки. Планы полов

Раскладка от чистовых размеров · размеры в мм · отметки от ±0,000

Фрагмент 1. Ванная комната (пом. 2). Пол 600×600, шов 2 мм, М 1:40

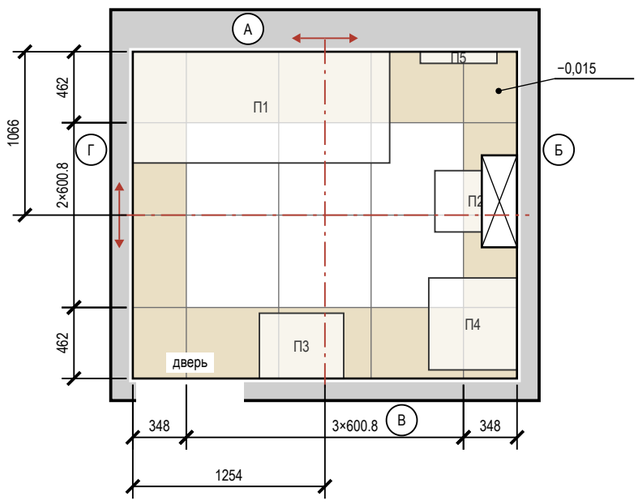

Фрагмент 2. Коридор (пом. 5). Пол 600×600, шов 2 мм, М 1:40

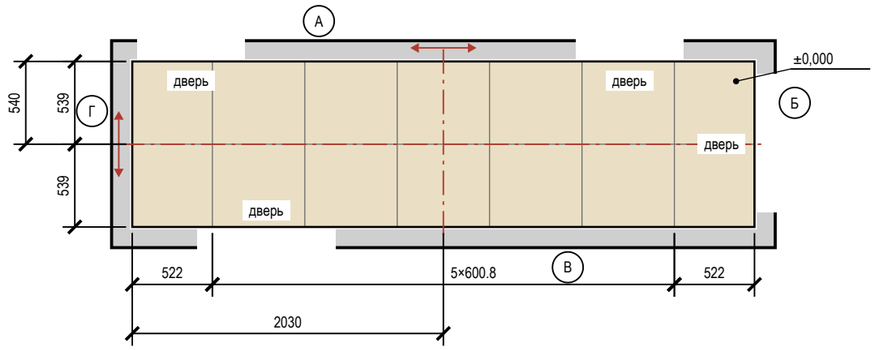

Фрагмент 3. Прихожая-коридор (пом. 7). Пол 600×600, шов 2 мм, М 1:40

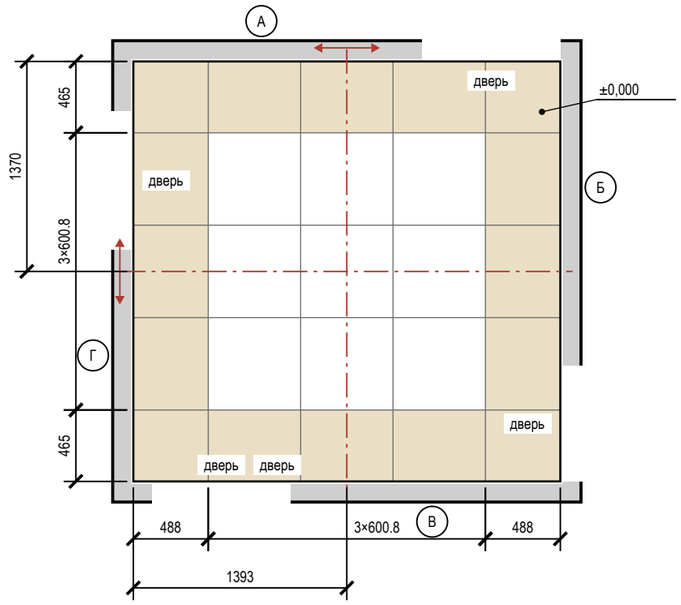

Фрагмент 4. Санузел (пом. 10). Пол 600×600, шов 2 мм, М 1:40

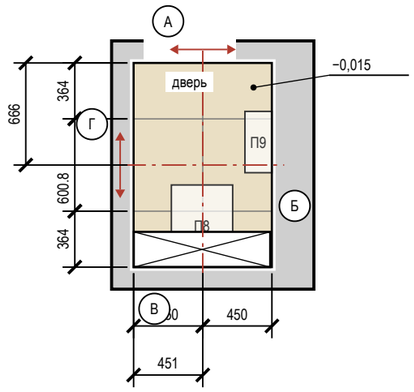

Условные обозначения

- плитка целая; тонкая линия — шов
- плитка с подрезкой (размер — на цепочке)
- ось старта; стрелки — направление укладки
- сантехприбор: габарит, высота по практике
- короб инсталляции: плитка пола — до короба
- отметка чистого пола на полке выноски, м
- А — обозначение стены А–Г (как на развёртках)

Допущения и предложения на листе

Основа листа: размеры сняты с размерных цепочек растрового скана плана заказчика, на объекте не замерены; ступени наружного контура приведены к граням помещений модели (ИЗ-8, К-20, К-21); высота потолка 2700 мм принята, источника нет (К-24); тип дома и перекрытие (монолит, плита 220 мм) приняты, источника нет (К-3); толщины стен приняты (250 и 120 мм), источника нет (К-21); мощность 15 кВт принята, технических условий нет (К-25).
Знак «**» — предложение проектировщика, заказчиком не утверждено (согласовать с заказчиком): К-26: пол пом. 2, 5, 7, 10, стены пом. 2, 10, плинтус пом. 5, 7 — артикул изделия не выбран: позиция описана характеристиками («аналог по характеристикам»), артикул выбирается при закупке.
Открытые вопросы и конфликты по листу: К-26.
См. лист открытых вопросов (лист 6, запись К-3; лист 7, записи К-20, К-21, К-24, К-25; лист 8, запись К-26; лист 10, запись ИЗ-8).

Ведомость материалов

Материал	Класс, код	Норма расхода	Кол-во
Затирка	CG2WA аналог: Mapei Ultracolor 133	(a+b)/ab·шов·t·1,6	5,6 кг
Затирка	CG2WA	(a+b)/ab·шов·t·1,6	0,1 кг
Клей	C2 TE S1 аналог: Litokol K80 Eco	1,5 кг/м²·мм, слой 5	425 кг (17 меш.)
Клей	C2 TE S1	1,5 кг/м²·мм, слой 5	10 кг (1 меш.)
Гидроизоляция	обмазочная, 2 слоя: пол, стены по периметру и зоны замачивания	по ТУ	16,2 м²
Демпф. лента	по периметру пола из плитки		29,1 м

Ведомость плитки

Помещение, поверхность	Плитка, код	Формат	Шов	S, м²	Целых	Подр.	С запасом
Ванная комната, пол	керамогранит матовый R10, тон J484	600.8×600.8	2	5,57	6	14	22
Ванная комната, стены А–Г	керамогранит матовый, тон F497	600.8×600.8	2	21,66	23	67	100
Ванная комната, короб инсталляции	керамогранит матовый, тон F497	600.8×600.8	2	1,36	1	6	8
Коридор, пол	керамогранит матовый R10, тон V486	600.8×600.8	2	4,54	0	14	16
Прихожая-коридор, пол	керамогранит матовый R10, тон V486	600.8×600.8	2	7,80	9	16	28
Санузел, пол	керамогранит матовый R10, тон J484	600.8×600.8	2	1,31	0	6	7
Санузел, стены А–Г	керамогранит матовый, тон F497	600.8×600.8	2	9,44	6	44	56
Санузел, короб инсталляции	керамогранит матовый, тон F497	600.8×600.8	2	1,76	0	10	11
Кухня, фартук (ст. А)	аналог: керамогранит матовый, тон F497	600.8×600.8	2	1,11	1	3	5
Итого 600.8×600.8				**54,54**	**46**	**180**	**253**

Примечания

1. Раскладка от чистовых размеров: стены санузлов теряют 10 + 5 + 9 = 24 мм на сторону (штукатурка, клей, плитка); подрезки — чистые, без шва.
2. Старт — от центра помещения (штрихпунктир, стрелки — направление укладки); размер старта — от чистовых стен Г и А.
3. Раскладка фартука «Кухня» — на листе «Раскладка плитки. Фартук кухни».
4. Количество: целые по раскладке + по одной на подрезку, запас 10 %; один артикул — одна партия и тон. Исключены поддон, короб, проёмы и места за коробом; S — по чистым граням: стены нетто = зона облицовки по ведомости отделки − место за коробом инсталляции 1,71 м² (плитку за коробом не кладут), короб — отдельной строкой.
5. Клей C2 TE S1 аналог: Litokol K80 Eco; C2 TE S1 (ГОСТ Р 56387-2018), затирка CG2WA аналог: Mapei Ultracolor 133; CG2WA; расход — по ТУ выбранной марки.
6. Гидроизоляция: пол и стены 200 мм от ЧП; над ванной — до 2100 и 300 мм за борт (см. развёртки); акт скрытых работ, пролив 24 ч.
7. Швы пола совмещены со швами стены А; по периметру — демпферная лента.
8. Отметка чистого пола −0,015, порог 15 мм; стык с соседним покрытием — по оси полотна двери.

1000 мм · печать 1:1

Изм.	Кол.уч	Лист	№ док.	Подп.	Дата
Разраб.		Кырлан А.С.			21.10.26
Пров.					
ГИП		Кырлан А.С.			21.10.26
Н. контр.					
Утв.					

ГД-2026-004-АИ

Четырёхкомнатная квартира

Общая площадь 102,67* м² · * размеры со скана, не замерены (реестр — л. 6–11, ИЗ-8, К-20, К-21)

Дизайн-проект интерьера четырёхкомнатной квартиры

Стадия	Лист	Листов
РП	49	124

Раскладка плитки. Планы полов

М 1:40

Кырлан Александр Сергеевич

выпуск 05.10.2026 № 7e7a2cd217 · стр. 57 из 168

Раскладка плитки. Фартук кухни

Раскладка от чистовых размеров · размеры в мм · высоты фартука от чистого пола

Фрагмент 1. Кухня (пом. 6), фартук, стена А. 600×600, шов 2 мм, М 1:20

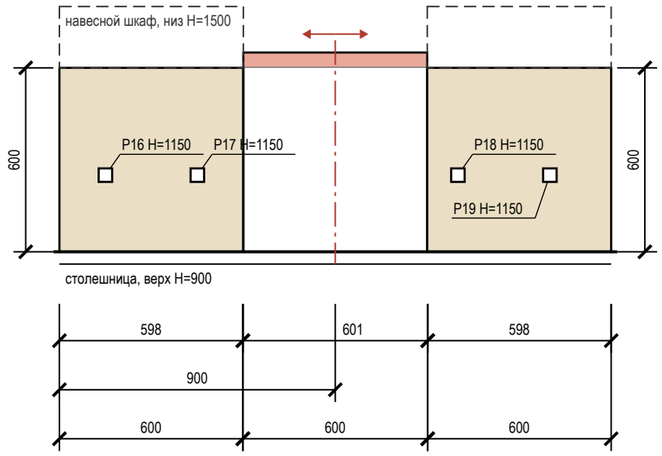

Условные обозначения

- плитка целая; тонкая линия — шов
- плитка с подрезкой (размер — на цепочке)
- ось старта; стрелки — направление укладки
- электроточка: марка и Н — по листам ЭОМ
- столешница (верх)
- навесной шкаф над фартуком

Подсчёт плитки

Поверхность	Формат	S, м²	Целых	Подр.	С запасом
Кухня, фартук (ст. А)	600×600	1,11	1	3	5

Сдвиг розеток фартука под раскладку

Точка (ЭОМ)	Проект: от угла / Н	Под раскладку: от угла / Н	Сдвиг, мм
Р16	150 / 1150	297 / 1200	+147 от шва; Н +50 ось ряда
Р17	450 / 1150	599 / 1200	+149 на шов; Н +50 ось ряда
Р18	1300 / 1150	1201 / 1200	−99 на шов; Н +50 ось ряда
Р19	1600 / 1150	1503 / 1200	−97 от шва; Н +50 ось ряда

Примечания

1. Фартук, Кухня: 600×600 горизонтально, шов 2 мм; зоны 600 мм — 900…1500, 600 мм — 900…1550, 600 мм — 900…1500 (от столешницы до низа навесного шкафа, без шкафа — 650 мм). Старт от центра участка, подрезки 598 мм. Площадь 1,11 м² — как в ведомости отделки.
2. Фартук — после монтажа столешницы, низ на 2–3 мм выше неё, шов со столешницей — санитарный герметик; навесные шкафы — после фартука. Торцы у пенала и стены — профиль или запил 45°.
3. Фартук, Кухня: в зоне до отм. 1550 верхний ряд подрезан 47 мм — меньше 1/3 плитки; полоса прикрыта корпусом навесного модуля и на виду не остаётся. Раскладкой не снимается: убрать подрезку можно, только выровняв низ этого модуля с соседними (1500 мм) — решение мебельщика.
4. Розетки из таблицы переносятся до черновой электрики: по высоте — на ось ряда плитки, от вертикального шва крупной плитки — не ближе 60 мм. Привязка — от левого края фартука на развёртке.
5. Клей, затирка и итог по форматам — в ведомостях листа «Раскладка плитки. Планы полов».

Допущения и предложения на листе

Основа листа: размеры сняты с размерных цепочек растрового скана плана заказчика, на объекте не замерены; ступени наружного контура приведены к граням помещений модели (ИЗ-8, К-20, К-21); высота потолка 2700 мм принята, источника нет (К-24); тип дома и перекрытие (монолит, плита 220 мм) приняты, источника нет (К-3); толщины стен приняты (250 и 120 мм), источника нет (К-21); мощность 15 кВт принята, технических условий нет (К-25).

Знак «**» — предложение проектировщика, заказчиком не утверждено (согласовать с заказчиком): К-26: пол пом. 6, плинтус пом. 6, фартук пом. 6 — артикул изделия не выбран: позиция описана характеристиками («аналог по характеристикам»), артикул выбирается при закупке.

Открытые вопросы и конфликты по листу: К-26.

См. лист открытых вопросов (лист 6, запись К-3; лист 7, записи К-20, К-21, К-24, К-25; лист 8, запись К-26; лист 10, запись ИЗ-8).

1000 мм · печать 1:1

Изм.	Кол.уч	Лист	№ док.	Подп.	Дата
Разраб.		Кырлан А.С.			21.10.26
Пров.					
ГИП		Кырлан А.С.			21.10.26
Н. контр.					
Утв.					

ГД-2026-004-АИ

Четырёхкомнатная квартира

Общая площадь 102,67* м² · * размеры со скана, не замерены (реестр — л. 6–11, ИЗ-8, К-20, К-21)

Дизайн-проект интерьера четырёхкомнатной квартиры

Стадия	Лист	Листов
РП	50	124

Раскладка плитки. Фартук кухни

М 1:20

Кырлан Александр Сергеевич

выпуск 05.10.2026 № 7e7a2cd217 · стр. 58 из 168

Раскладка плитки. Ванная комната. Развёртки стен

ПРЕДВАРИТЕЛЬНО · не для производства работ · открыто пунктов: 30 (реестр — л. 6–11)

Пом. 2 · вид изнутри помещения · размеры в мм · высоты от чистого пола, отметки от ±0,000

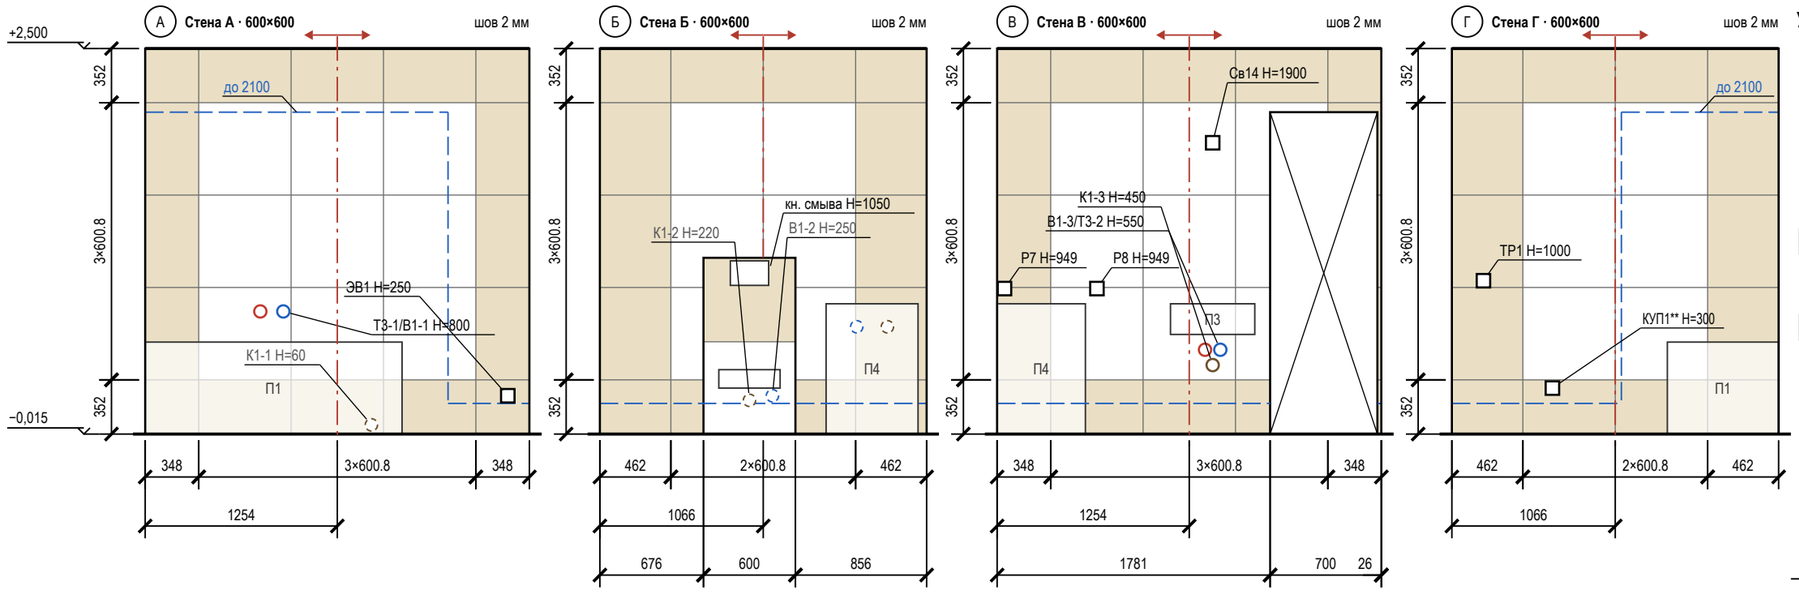

Условные обозначения

- плитка целая; тонкая линия — шов
- плитка с подрезкой (размер — на цепочке)
- ось старта; стрелки — направление укладки
- верх гидроизоляции: 200 от ЧП, в мокрой зоне — «до …»
- проём — не облицовывается
- сантехприбор: габарит, высота по практике
- короб инсталляции, в нём кнопка смыва 250×160
- вывод В1 (код — в ведомости привязок)
- вывод ТЗ (код — в ведомости привязок)
- вывод К1 (код — в ведомости привязок)
- вывод за прибором / в коробе (не на сетке)
- электроточка: марка и Н — по листам ЭОМ
- отметка уровня, м: ±0,000 — чистый пол жилых помещений
- низ потолка; серая полоса — стена без плитки
- А — обозначение стены А–Г (как на развёртках)

Подсчёт плитки по стенам и коробу

Поверхность	L × H, мм	S, м²	Целых	Подр.	С запасом	Подрезки: край / верх, мм
стена А	2507 × 2515	6,43	9	16	28	348 / 348; 352
стена Б	2132 × 2515	4,79	2	18	22	462 / 462; 352
короб (ст. Б)	600×1150×230	1,36	1	6	8	лицо 600; бок. 230
стена В	2507 × 2515	4,96	6	19	28	348 / 348; 352
стена Г	2132 × 2515	5,48	6	14	22	462 / 462; 352
Итого		**23,01**	**24**	**73**	**108**	

Сдвиг точек под раскладку

Точка (ВК, ЭОМ)	Стена	Проект: от угла / Н	Под раскладку: от угла / Н	Сдвиг, мм
ТЗ-1/В1-1	А	826 / 800	952 / 655	+126 на шов; Н −145
ЭВ1	А	2366 / 250	2459 / 353	+93 в центр плитки; Н +103
В1-3/ТЗ-2	В	1406 / 550	1555 / 655	+149 на шов; Н +105
К1-3	В	1406 / 450	1253 / 353	−153 в центр плитки; Н −97
Св14	В	1406 / 1900	1555 / 1860	+149 на шов; Н −40
ТР1	Г	206 / 1000	162 / 956	−44 в центр плитки; Н −44
КУП1**	Г	656 / 300	765 / 353	+109 в центр плитки; Н +53

Примечания

1. Вид изнутри, стены по часовой стрелке А → Г. Высоты — от чистого пола (−0,015), отметки — от ±0,000. Раскладка от чистовых размеров (штукатурка 10 + клей 5 + плитка 9 мм), подрезки чистые; старт — от оси стены, ряды от середины (две подрезки).
2. Облицовка до потолка (+2,500).
3. Точки из таблицы сдвигов переносятся до черновой разводки: смеситель — по оси пары В1 + ТЗ; вывод на оси прибора — вместе с прибором, иначе старт раскладки — на ось прибора.
4. Выводы — по «Плану выводов сантехники», электроточки — по ЭОМ, «*» — высота по практике; за приборами и в коробе (К1-1, В1-2, К1-2, В1-4, К1-4) — штриховым кольцом.
5. Гидроизоляция: 200 мм от ЧП по периметру; над ванной — до 2100 и 300 мм за борт (СП 29.13330.2011, п. 7.2 — на высоту замачивания); углы — лентой; акт скрытых работ, пролив.
6. Короб 600×1150×230: лицо 600 мм от оси кнопки смыва, боковины, полка; углы — запил 45° или профиль; за коробом плитку не кладут.
7. Наружные углы: ст. Б: 2 — запил 45°; ст. В: 2 — профиль.
8. Люки: Л1 (ст. Б, 600×600, нажимной) — кромки дверцы по швам сетки.

Допущения и предложения на листе

Основа листа: размеры сняты с размерных цепочек растрового скана плана заказчика, на объекте не замерены; ступени наружного контура приведены к граням помещений модели (ИЗ-8, К-20, К-21); высота потолка 2700 мм принята, источника нет (К-24); тип дома и перекрытие (монолит, плита 220 мм) приняты, источника нет (К-3); толщины стен приняты (250 и 120 мм), источника нет (К-21); мощность 15 кВт принята, технических условий нет (К-25).

Знак «**» — предложение проектировщика, заказчиком не утверждено (согласовать с заказчиком): ИЗ-8: дверь пом. 2 (стена В) — смещение 100 → 110 мм (откос до угла был 40 мм при норме от 50 мм); ИЗ-12: КУП1 — коробка уравнивания потенциалов, проводник от шины РЕ; К-26: пол пом. 2, стены пом. 2 — артикул изделия не выбран: позиция описана характеристиками («аналог по характеристикам»), артикул выбирается при закупке.

Открытые вопросы и конфликты по листу: К-26.

См. лист открытых вопросов (лист 6, запись К-3; лист 7, записи К-20, К-21, К-24, К-25; лист 8, запись К-26; лист 10, записи ИЗ-8, ИЗ-12).

1000 мм · печать 1:1

Изм.	Кол.уч	Лист	№ док.	Подп.	Дата
Разраб.		Кырлан А.С.			21.10.26
Пров.					
ГИП		Кырлан А.С.			21.10.26
Н. контр.					
Утв.					

ГД-2026-004-АИ

Четырёхкомнатная квартира

Общая площадь 102,67* м² · * размеры со скана, не замерены (реестр — л. 6–11, ИЗ-8, К-20, К-21)

Дизайн-проект интерьера четырёхкомнатной квартиры

Стадия	Лист	Листов
РП	51	124

Раскладка плитки. Ванная комната. Развёртки стен

М 1:40

Кырлан Александр Сергеевич

выпуск 05.10.2026 № 7e7a2cd217 · стр. 59 из 168

Раскладка плитки. Санузел. Развёртки стен

Пом. 10 · вид изнутри помещения · размеры в мм · высоты от чистого пола, отметки от ±0,000

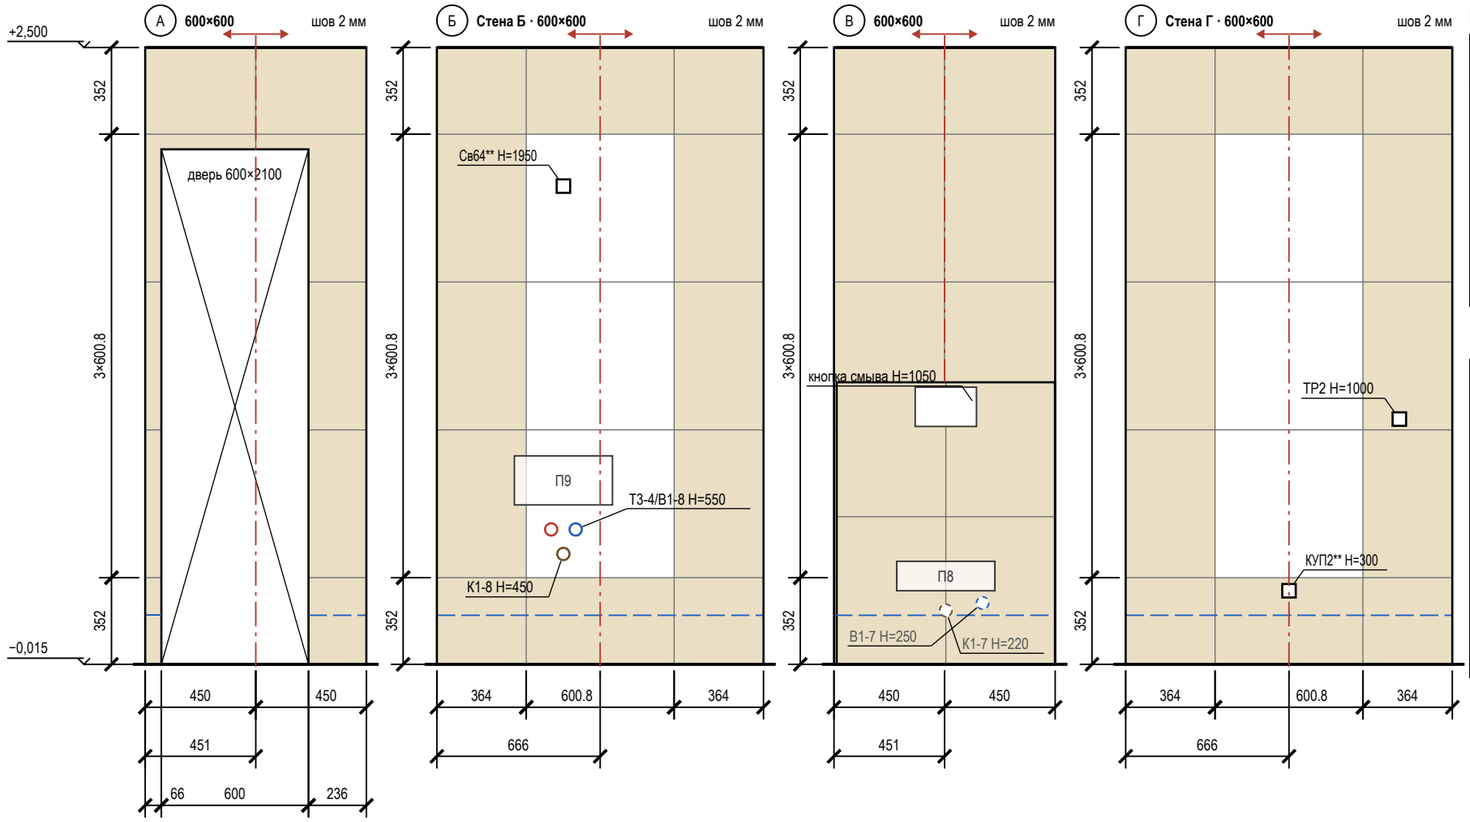

Подсчёт плитки по стенам и коробу

Поверхность	L × H, мм	S, м²	Целых	Подр.	С запасом	Подрезки: край / верх, мм
стена А	902 × 2515	1,13	0	10	11	450 / 450; 352
стена Б	1332 × 2515	3,47	3	12	17	364 / 364; 352
стена В	902 × 2515	1,37	0	10	11	450 / 450; 352
короб (ст. В)	890×1150×230	1,76	0	10	11	лицо 444 / 444; бок. 230
стена Г	1332 × 2515	3,47	3	12	17	364 / 364; 352
Итого		**11,19**	**6**	**54**	**67**	

Сдвиг точек под раскладку

Точка (ВК, ЭОМ)	Стена	Проект: от угла / H	Под раскладку: от угла / H	Сдвиг, мм
Т3-4/В1-8	Б	516 / 550	666 / 655	+150 в центр плитки; H +105
К1-8	Б	516 / 450	666 / 353	+150 в центр плитки; H −97
Св64**	Б	516 / 1950	666 / 1860	+150 в центр плитки; H −90
КУП2**	Г	666 / 300	666 / 353	H +53
ТР2	Г	1116 / 1000	1269 / 956	+153 в центр плитки; H −44

Условные обозначения

- плитка целая; тонкая линия — шов
- плитка с подрезкой (размер — на цепочке)
- ось старта; стрелки — направление укладки
- верх гидроизоляции: 200 от ЧП, в мокрой зоне — «до …»
- проём — не облицовывается
- сантехприбор: габарит, высота по практике
- короб инсталляции, в нём кнопка смыва 250×160
- вывод В1 (код — в ведомости привязок)
- вывод Т3 (код — в ведомости привязок)
- вывод К1 (код — в ведомости привязок)
- вывод за прибором / в коробе (не на сетке)
- электроточка: марка и H — по листам ЭОМ
- отметка уровня, м: ±0,000 — чистый пол жилых помещений
- низ потолка; серая полоса — стена без плитки
- (А) обозначение стены А–Г (как на развёртках)

1000 мм · печать 1:1

Примечания

1. Вид изнутри, стены по часовой стрелке А → Г. Высоты — от чистого пола (−0,015), отметки — от ±0,000. Раскладка от чистовых размеров (штукатурка 10 + клей 5 + плитка 9 мм), подрезки чистые; старт — от оси стены, ряды от середины (две подрезки).
2. Облицовка до потолка (+2,500).
3. Точки из таблицы сдвигов переносятся до черновой разводки: смеситель — по оси пары В1 + Т3; вывод на оси прибора — вместе с прибором, иначе старт раскладки — на ось прибора.
4. Выводы — по «Плану выводов сантехники», электроточки — по ЭОМ, «*» — высота по практике; за приборами и в коробе (В1-7, К1-7) — штриховым кольцом.
5. Гидроизоляция: 200 мм от ЧП по периметру; углы — лентой; акт скрытых работ, пролив.
6. Короб 890×1150×230: лицо 444 / 444 мм от оси кнопки смыва, боковины, полка; углы — запил 45° или профиль; за коробом плитку не кладут.
7. Между коробом и углом полоса 11 мм — довести короб до угла.
8. Наружные углы: ст. А: 2 — профиль.

Допущения и предложения на листе

Основа листа: размеры сняты с размерных цепочек растрового скана плана заказчика, на объекте не замерены; ступени наружного контура приведены к граням помещений модели (ИЗ-8, К-20, К-21); высота потолка 2700 мм принята, источника нет (К-24); тип дома и перекрытие (монолит, плита 220 мм) приняты, источника нет (К-3); толщины стен приняты (250 и 120 мм), источника нет (К-21); мощность 15 кВт принята, технических условий нет (К-25).

Знак «**» — предложение проектировщика, заказчиком не утверждено (согласовать с заказчиком): ИЗ-3: Св64; ИЗ-12: КУП2 — коробка уравнивания потенциалов, проводник от шины РЕ; К-26: пол пом. 10, стены пом. 10 — артикул изделия не выбран: позиция описана характеристиками («аналог по характеристикам»), артикул выбирается при закупке.

Открытые вопросы и конфликты по листу: К-26.

См. лист открытых вопросов (лист 6, запись К-3; лист 7, записи К-20, К-21, К-24, К-25; лист 8, запись К-26; лист 9, запись ИЗ-3; лист 10, записи ИЗ-8, ИЗ-12).

Изм.	Кол.уч	Лист	№ док.	Подп.	Дата
Разраб.		Кырлан А.С.			21.10.26
Пров.					
ГИП		Кырлан А.С.			21.10.26
Н. контр.					
Утв.					

ГД-2026-004-АИ

Четырёхкомнатная квартира

Общая площадь 102,67* м² · * размеры со скана, не замерены (реестр — л. 6–11, ИЗ-8, К-20, К-21)

Дизайн-проект интерьера четырёхкомнатной квартиры

Стадия	Лист	Листов
РП	52	124

Раскладка плитки. Санузел. Развёртки стен

М 1:25

Кырлан Александр Сергеевич

выпуск 05.10.2026 № 7e7a2cd217 · стр. 60 из 168

07

Полы и отделка

Кырлан Александр Сергеевич

выпуск 05.10.2026 · № 7e7a2cd217 · стр. 61 из 168

План полов

Покрытия, направление укладки, отметки чистого пола, стыки · размеры в мм · отметки в м

ПРЕДВАРИТЕЛЬНО · не для производства работ · открыто пунктов: 30 (реестр — л. 6–11)

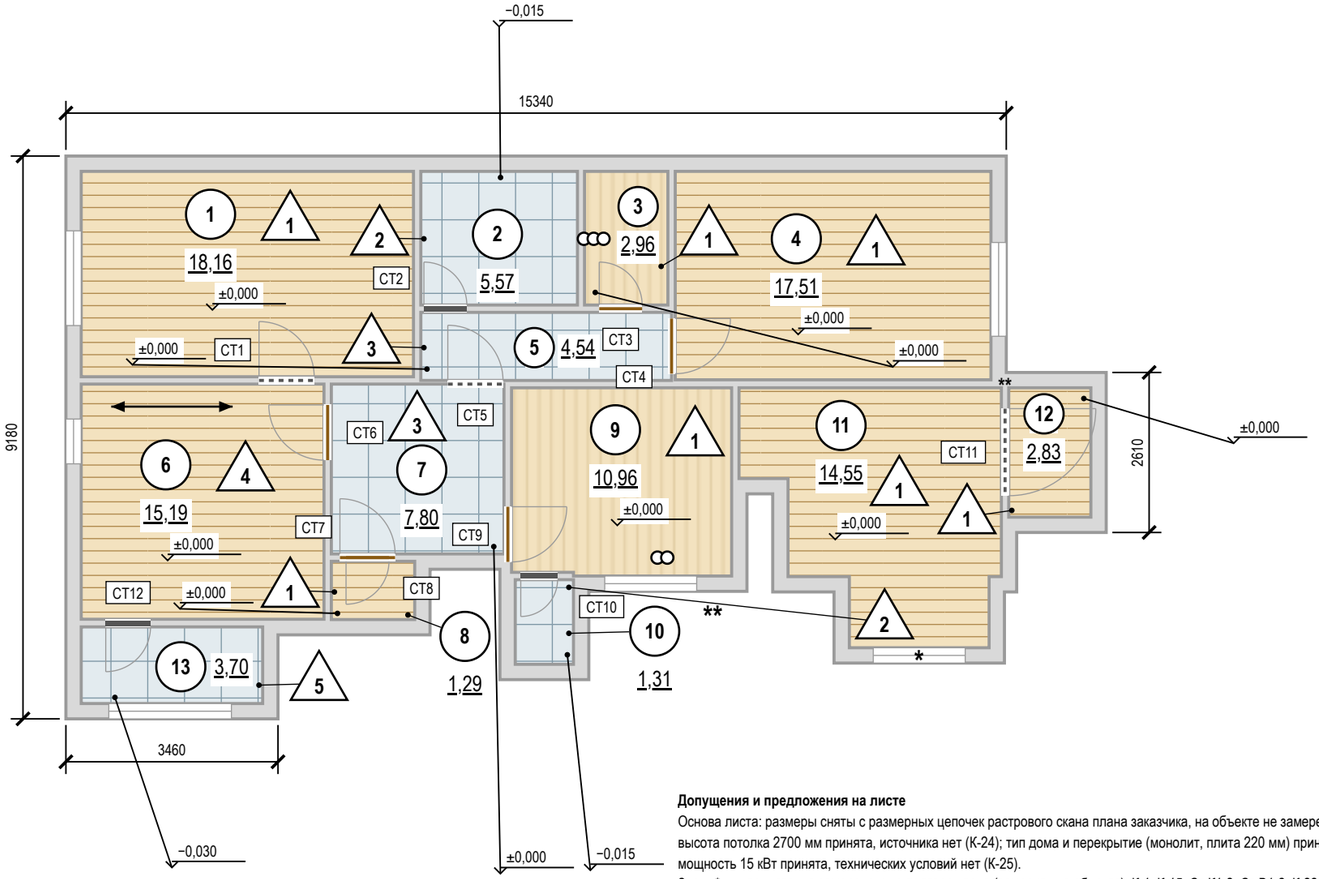

Условные обозначения

- тип 1 — инженерная доска, линии — вдоль доски
- тип 2 — керамогранит 600×600, сетка — формат плитки
- тип 3 — керамогранит 600×600, сетка — формат плитки
- тип 4 — инженерная доска, линии — вдоль доски
- тип 5 — керамогранит
- 1 — номер типа пола (экспликация полов)
- схема пола, без масштаба: плита — штриховка, стяжка — точки, звукоизоляция — зигзаг, гидроизоляция — утолщённая линия с заведением на стену
- направление укладки (длинная сторона доски)
- отметка чистого пола, м
- стык в проёме: без порога (б/п)
- стык в проёме: порог
- стык в проёме: Т-профиль по оси полотна
- CT1 — марка стыка (ведомость стыков)
- стояк: К1 — канализация, В1 — ХВС, Т3 — ГВС
- 1 — номер помещения, площадь м²

Отметки по высоте

±0,000	чистый пол пом. 1, 3–9, 11, 12; отсчёт высот
−0,015	чистый пол пом. 2, 10, ниже на 15 мм
−0,030	чистый пол пом. 13, ниже на 30 мм
−0,170*	верх плиты — расчёт, не замер (задание на обмер)
сущ. пол	снимается до плиты; не замерен (задание на обмер)

Допущения и предложения на листе

Основа листа: размеры сняты с размерных цепочек растрового скана плана заказчика, на объекте не замерены; ступени наружного контура приведены к граням помещений модели (ИЗ-8, К-20, К-21); высота потолка 2700 мм принята, источника нет (К-24); тип дома и перекрытие (монолит, плита 220 мм) приняты, источника нет (К-3); толщины стен приняты (250 и 120 мм), источника нет (К-21); мощность 15 кВт принята, технических условий нет (К-25).

Знак «*» — принято, не замерено и не подтверждено (замерить на объекте): К-1, К-15: Ст К1-2, Ст В1-2; К-22: окно пом. 11 (стена В).

Знак «**» — предложение проектировщика, заказчиком не утверждено (согласовать с заказчиком): ИЗ-1, К-1: окно пом. 9 (стена В); ИЗ-1, К-26: пол пом. 9 — направление паркета изменено вслед за окном: по оси X → по оси Y; артикул изделия не выбран: позиция описана характеристиками («аналог по характеристикам»), артикул выбирается при закупке; ИЗ-6: дверь пом. 12 (стена Г); ИЗ-8: дверь пом. 2 (стена В) — смещение 100 → 110 мм (откос до угла был 40 мм при норме от 50 мм); К-26: пол пом. 1–8, 10–13, плинтус пом. 1, 3–9, 11–13, акцент пом. 1, 11, стены пом. 2, 10, фартук пом. 6 — артикул изделия не выбран: позиция описана характеристиками («аналог по характеристикам»), артикул выбирается при закупке.

Открытые вопросы и конфликты по листу: К-26.

См. лист открытых вопросов (лист 6, записи К-1, К-3; лист 7, записи К-15, К-20–К-22, К-24, К-25; лист 8, запись К-26; лист 9, записи ИЗ-1, ИЗ-6; лист 10, запись ИЗ-8).

Примечания

1. За отметку ±0,000 принят чистый пол, не существующий (блок отметок). Площади — по чистым размерам помещений, м²; размеры — в мм.
2. Стык разнотипных покрытий — по оси дверного полотна (под полотном в закрытом положении); решение стыка — по ведомости стыков.
3. Пол санузлов ниже смежных помещений на 15 мм за счёт меньшей толщины стяжки (верх плиты общий — по экспликации полов); гидроизоляция по стяжке с заведением на стены не менее 200 мм (СП 29.13330.2011, п. 7.2), до облицовки — тест проливом и акт скрытых работ.
4. Выпуски канализации с уклоном и трассы водоснабжения — в слое засыпки под стяжкой (по экспликации полов); отметки, уклоны и прочистки — по листу разводки ВК 41.
5. Штучные покрытия (инженерная доска): направление — по стрелке; влажность основания по СМ не более 2,0 % (по ТУ изготовителя).
6. Ровность основания — просвет под 2-метровой рейкой не более 2 мм: пом. 1, 3, 4, 6, 8, 9, 11, 12 (инженерная доска), пом. 2, 5, 7, 10 (керамогранит); 3 мм: пом. 13 (керамогранит); проверить до укладки покрытия (СП 71.13330.2017, табл. 8.5).
7. Плавающая стяжка по звукоизоляции: демпферная (кромочная) лента по контуру помещения, у стояков и колонн — до верха чистого пола (СП 51.13330.2011, п. 9.11); плинтус крепится только к стене.
8. Сетка на плитке — условная, в размер формата; точка старта и раскладка — по листу раскладки плитки.
9. Узор покрытия (заливка-код типа пола) прерывается под надписями — площадями помещений и отметками чистого пола.
10. Пироги полов — по экспликации полов: слои сверху вниз, толщины в мм; гидроизоляция мокрых зон — в пироге и в ведомости отделки; схема пола — без масштаба.
11. Экспликация полов (ф. 4 прил. А ГОСТ 21.501-2018) и ведомость стыков покрытий — на отдельном листе 54.

1000 мм · печать 1:1

Изм.	Кол.уч	Лист	№ док.	Подп.	Дата
Разраб.		Кырлан А.С.			21.10.26
Пров.					
ГИП		Кырлан А.С.			21.10.26
Н. контр.					
Утв.					

ГД-2026-004-АИ

Четырёхкомнатная квартира

Общая площадь 102,67* м² · * размеры со скана, не замерены (реестр — л. 6–11, ИЗ-8, К-20, К-21)

Дизайн-проект интерьера четырёхкомнатной квартиры

Стадия	Лист	Листов
РП	53	124

План полов

М 1:100

Кырлан Александр Сергеевич

выпуск 05.10.2026 № 7e7a2cd217 · стр. 62 из 168

Конструкции полов и стыки покрытий

Форма 4 прил. А ГОСТ 21.501-2018 · толщины в мм · отметки в м

ПРЕДВАРИТЕЛЬНО · не для производства работ · открыто пунктов: 30 (реестр — л. 6–11)

Экспликация полов

Номер помещения	Тип пола	Схема пола	Данные элементов пола (наименование, толщина, основание), мм	Площадь, м²
1, 3, 4, 8, 9, 11, 12	1	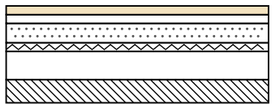	Инженерная доска дуб на клею — 14 Клей паркетный МС-полимерный — 1 Стяжка ЦПС М300 (В22,5), фибра, по звукоизоляции — 55 Звукоизоляция — минплита 110 кг/м³ — 20 Засыпка керамзитовая фр. 0–5, уплотнённая — 80 Плита перекрытия монолитная Всего 170 мм; ЧП ±0,000, верх плиты −0,170	68,26
2, 10	2	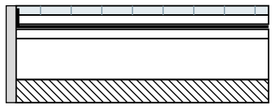	Керамогранит 600×600×10 — 10 Нагревательный мат в слое клея С2 TE S1 — 8 Гидроизоляция обмазочная, 2 слоя (заход на стены — по ведомости отделки) — 2 Сборное основание ГВЛВ 2×12,5 — 25 Засыпка керамзитовая сухая фр. 0–5 (в слое — выпуски К1) — 110 Плита перекрытия монолитная Всего 155 мм; ЧП −0,015, верх плиты −0,170	6,88
5, 7	3	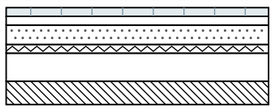	Керамогранит 600×600×10 — 10 Клей плиточный С2 TE S1 — 5 Стяжка ЦПС М300 (В22,5), фибра, по звукоизоляции — 55 Звукоизоляция — минплита 110 кг/м³ — 20 Засыпка керамзитовая фр. 0–5, уплотнённая — 80 Плита перекрытия монолитная Всего 170 мм; ЧП ±0,000, верх плиты −0,170	12,34
6	4	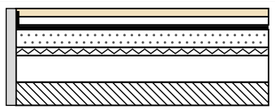	Инженерная доска дуб на клею — 14 Клей паркетный МС-полимерный — 1 Гидроизоляция полиуретановая, 2 слоя (зона мойки и острова) — 2 Стяжка ЦПС М300 (В22,5), фибра, по звукоизоляции — 53 Звукоизоляция — минплита 110 кг/м³ — 20 Засыпка керамзитовая фр. 0–5, уплотнённая — 80 Плита перекрытия монолитная Всего 170 мм; ЧП ±0,000, верх плиты −0,170	15,19
13	5	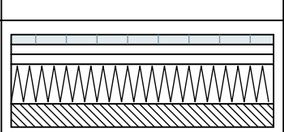	Керамогранит 600×600×10 — 10 Клей плиточный С2 TE S1 (деформируемый) — 5 Сборное основание ГВЛВ 2×12,5 — 25 Пенополистирол экструзионный 2×50 — 100 Плита перекрытия монолитная Всего 140 мм; ЧП −0,030, верх плиты −0,170	3,70
			Итого	**106,37**

Стыки покрытий в проёмах

Марка	Проём	Типы пола	Отметки ЧП	Решение
СТ1	1–6	1 / 4	±0,000 / ±0,000	б/п
СТ2	2–5	2 / 3	−0,015 / ±0,000	порог h=15 мм
СТ3	3–5	1 / 3	±0,000 / ±0,000	Т-профиль
СТ4	4–5	1 / 3	±0,000 / ±0,000	Т-профиль
СТ5	5–7	3 / 3	±0,000 / ±0,000	б/п
СТ6	6–7	4 / 3	±0,000 / ±0,000	Т-профиль
СТ7	7–8	3 / 1	±0,000 / ±0,000	Т-профиль
СТ8	8–7	1 / 3	±0,000 / ±0,000	Т-профиль
СТ9	9–7	1 / 3	±0,000 / ±0,000	Т-профиль
СТ10	10–9	2 / 1	−0,015 / ±0,000	порог h=15 мм
СТ11	12–11	1 / 1	±0,000 / ±0,000	б/п
СТ12	13–6	5 / 4	−0,030 / ±0,000	порог h=30 мм

Условные обозначения

- схема пола, без масштаба: плита — штриховка, стяжка — точки, звукоизоляция — зигзаг, гидроизоляция — утолщённая линия с заведением на стену
- стык в проёме: без порога (б/п)
- стык в проёме: порог
- стык в проёме: Т-профиль по оси полотна
- СТ1 — марка стыка (ведомость стыков)

Примечания

1. Экспликация полов — по форме 4 прил. А ГОСТ 21.501-2018: слои пирога сверху вниз, толщины в мм; схема пола — без масштаба.
2. Номера помещений, площади, отметки чистого пола, направление укладки и места стыков — по листу «План полов»; привязка марок стыков (СТ) на плане полов, тип каждой схемы пола — в строке экспликации.
3. Стык разнотипных покрытий — по оси дверного полотна (под полотном в закрытом положении).
4. Плавающая стяжка по звукоизоляции: демпферная (кромочная) лента по контуру помещения, у стояков и колонн — до верха чистого пола (СП 51.13330.2011, п. 9.11); плинтус крепится только к стене.
5. Гидроизоляция мокрых зон — с заведением на стены не менее 200 мм (СП 29.13330.2011, п. 7.2); до облицовки — тест проливом и акт скрытых работ.

Допущения и предложения на листе

Основа листа: размеры сняты с размерных цепочек растрового скана плана заказчика, на объекте не замерены; ступени наружного контура приведены к граням помещений модели (ИЗ-8, К-20, К-21); высота потолка 2700 мм принята, источника нет (К-24); тип дома и перекрытие (монолит, плита 220 мм) приняты, источника нет (К-3); толщины стен приняты (250 и 120 мм), источника нет (К-21); мощность 15 кВт принята, технических условий нет (К-25).

См. лист открытых вопросов (лист 6, запись К-3; лист 7, записи К-20, К-21, К-24, К-25; лист 10, запись ИЗ-8).

Изм.	Кол.уч	Лист	№ док.	Подп.	Дата
Разраб.		Кырлан А.С.			21.10.26
Пров.					
ГИП		Кырлан А.С.			21.10.26
Н. контр.					
Утв.					

ГД-2026-004-АИ

Четырёхкомнатная квартира

Общая площадь 102,67* м² · * размеры со скана, не замерены (реестр — л. 6–11, ИЗ-8, К-20, К-21)

Дизайн-проект интерьера четырёхкомнатной квартиры

Стадия	Лист	Листов
РП	54	124

Конструкции полов и стыки покрытий

М б/м

Кырлан Александр Сергеевич

выпуск 05.10.2026 № 7e7a2cd217 · стр. 63 из 168

Ведомость отделки помещений. Лист 1 из 3

Потолки, стены, низ стен, полы · площади в м², длины в м · отметки в м

Ведомость отделки помещений (форма 1 прил. А ГОСТ 21.501-2018). Лист 1 из 3

№	Наименование помещения	Потолок			Стены и перегородки			Низ стен (плинтус)			Пол		Примечание
		Вид отделки	Код цвета	S, м²	Вид отделки	Код цвета	S, м²	Вид отделки	Код цвета	L, м	Вид отделки	S, м²	
1	Зал 18,16 м²	ГКЛ по каркасу П113, отм. +2,500; +2,600; окраска, Tikkurila Anti-Reflex 2, глубокоматовая, 2 слоя, подготовка Q3	Tikkurila F497	18,16	Окраска, Tikkurila Optiva 5 Matt, матовая, 2 слоя, подготовка К3 Акцент — стена А: окраска, Tikkurila Optiva 5 Matt, матовая, 3 слоя, подготовка К3	Tikkurila F497 Tikkurila L481	25,94 13,55	Плинтус МДФ h=80 мм, аналог: МДФ под окраску 80×16 мм	Tikkurila F497	16,6	Инженерная доска, аналог: дуб натуральный брашированный, масло-воск, 14/4 мм, на клею; тип 1, отм. ЧП ±0,000	18,16	Н стен 2500 (до потолка); колеруется в код стен, но по эмали на МДФ: сличать отдельным выкрасом на своей подложке (выкрас № 10); плинтус в цвет: стены
2	Ванная комната 5,57 м²	ГКЛВ по каркасу П113, отм. +2,500; окраска, Tikkurila Luja 7, матовая, 2 слоя, подготовка Q3	Tikkurila F497	5,57	Облицовка плиткой, аналог: керамогранит матовый, тон F497, 600×600×9 мм, клей С2 TE S1, затирка CG2WA	#F1F1EC	22,35	нет (облицовка от пола)			Аналог: керамогранит матовый R10, тон J484, 600×600×10 мм; тип 2, отм. ЧП −0,015	5,57	Н стен 2515 (до потолка); тёплый пол; гидроизоляция обмазочная, 2 слоя, по всему помещению, с заведением на стены 200 мм, в душе — на 2100 мм и 500 мм за кабину (по пирогу пола); тест проливом и акт скрытых работ; облицовка от чистого пола до низа потолка; по ГКЛВ каркаса П113, влагостойкая окраска; Q3
3	Тёмная комната 2,96 м²	ГКЛ по каркасу П113, отм. +2,600; окраска, Tikkurila Anti-Reflex 2, глубокоматовая, 2 слоя, подготовка Q3	Tikkurila F497	2,96	Окраска, Tikkurila Optiva 5 Matt, матовая, 2 слоя, подготовка К3	Tikkurila F497	16,94	Плинтус МДФ h=80 мм, аналог: МДФ под окраску 80×16 мм	Tikkurila F497	6,4	Инженерная доска, аналог: дуб натуральный брашированный, масло-воск, 14/4 мм, на клею; тип 1, отм. ЧП ±0,000	2,96	Н стен 2600 (до потолка); колеруется в код стен, но по эмали на МДФ: сличать отдельным выкрасом на своей подложке (выкрас № 10); плинтус в цвет: стены
4	Детская 1 17,51 м²	ГКЛ по каркасу П113, отм. +2,600; окраска, Tikkurila Anti-Reflex 2, глубокоматовая, 2 слоя, подготовка Q3	Tikkurila F497	17,51	Окраска, Tikkurila Joker, полуматовая, 2 слоя, подготовка К3	Tikkurila F497	40,12	Плинтус МДФ h=80 мм, аналог: МДФ под окраску 80×16 мм	Tikkurila F497	16,2	Инженерная доска, аналог: дуб натуральный брашированный, масло-воск, 14/4 мм, на клею; тип 1, отм. ЧП ±0,000	17,51	Н стен 2600 (до потолка); колеруется в код стен, но по эмали на МДФ: сличать отдельным выкрасом на своей подложке (выкрас № 10); плинтус в цвет: стены
5	Коридор 4,54 м²	ГКЛ по каркасу П113, отм. +2,600; окраска, Tikkurila Anti-Reflex 2, глубокоматовая, 2 слоя, подготовка Q3	Tikkurila F497	4,54	Окраска, Tikkurila Optiva 20 Semimatt, полуматовая, 2 слоя, подготовка К3	Tikkurila J484	22,21	Плинтус МДФ h=80 мм, аналог: МДФ под окраску 80×16 мм	Tikkurila J484	8,1	Аналог: керамогранит матовый R10, тон V486, 600×600×10 мм; тип 3, отм. ЧП ±0,000	4,54	Н стен 2600 (до потолка); колеруется в код стен, но по эмали на МДФ: сличать отдельным выкрасом на своей подложке (выкрас № 10); плинтус в цвет: стены

Примечания

1. Ведомость продолжена на листе 2 из 3; итоги, сводка площадей и примечания — на последнем листе ведомости.

Допущения и предложения на листе

Основа листа: размеры сняты с размерных цепочек растрового скана плана заказчика, на объекте не замерены; ступени наружного контура приведены к граням помещений модели (ИЗ-8, К-20, К-21); высота потолка 2700 мм принята, источника нет (К-24); тип дома и перекрытие (монолит, плита 220 мм) приняты, источника нет (К-3); толщины стен приняты (250 и 120 мм), источника нет (К-21); мощность 15 кВт принята, технических условий нет (К-25).

Знак «**» — предложение проектировщика, заказчиком не утверждено (согласовать с заказчиком): ИЗ-1, К-26: пол пом. 9 — направление паркета изменено вслед за окном: по оси X → по оси Y; артикул изделия не выбран: позиция описана характеристиками («аналог по характеристикам»), артикул выбирается при закупке; К-26: пол пом. 1–8, 10–13, плинтус пом. 1, 3–9, 11–13, акцент пом. 1, 11, стены пом. 2, 10, фартук пом. 6 — артикул изделия не выбран: позиция описана характеристиками («аналог по характеристикам»), артикул выбирается при закупке.

Открытые вопросы и конфликты по листу: К-26.

См. лист открытых вопросов (лист 6, запись К-3; лист 7, записи К-20, К-21, К-24, К-25; лист 8, запись К-26; лист 9, запись ИЗ-1; лист 10, запись ИЗ-8).

Изм.	Кол.уч	Лист	№ док.	Подп.	Дата
Разраб.		Кырлан А.С.			21.10.26
Пров.					
ГИП		Кырлан А.С.			21.10.26
Н. контр.					
Утв.					

ГД-2026-004-АИ

Четырёхкомнатная квартира

Общая площадь 102,67* м² · * размеры со скана, не замерены (реестр — л. 6–11, ИЗ-8, К-20, К-21)

Дизайн-проект интерьера четырёхкомнатной квартиры

Стадия	Лист	Листов
РП	55	124

Ведомость отделки помещений. Лист 1 из 3

М б/м

Кырлан Александр Сергеевич

выпуск 05.10.2026 № 7e7a2cd217 · стр. 64 из 168

Ведомость отделки помещений. Лист 2 из 3

Потолки, стены, низ стен, полы · площади в м², длины в м · отметки в м

Ведомость отделки помещений (форма 1 прил. А ГОСТ 21.501-2018). Лист 2 из 3

№	Наименование помещения	Потолок			Стены и перегородки			Низ стен (плинтус)			Пол		Примечание
		Вид отделки	Код цвета	S, м²	Вид отделки	Код цвета	S, м²	Вид отделки	Код цвета	L, м	Вид отделки	S, м²	
6	Кухня 15,19 м²	ГКЛ по каркасу П113, отм. +2,600; окраска, Tikkurila Luja 7, матовая, 2 слоя, подготовка Q3	Tikkurila F497	15,19	Окраска, Tikkurila Luja 7, полуматовая, 2 слоя, подготовка К3 Фартук кухни (стена А): облицовка керамогранитом, аналог: керамогранит матовый, тон F497, 600×600×9 мм, клей C2 TE S1, затирка CG2WA	Tikkurila F497 #F1F1EC	34,48 1,11	Плинтус МДФ h=80 мм, аналог: МДФ под окраску 80×16 мм	Tikkurila F497	13,8	Инженерная доска, аналог: дуб натуральный брашированный, масло-воск, 14/4 мм, на клею; тип 4, отм. ЧП ±0,000	15,19	Н стен 2600 (до потолка); гидроизоляция обмазочная, 2 слоя, с заведением на стены 200 мм (по пирогу пола); тест проливом и акт скрытых работ; влагостойкая полуматовая окраска (класс мокрого истирания 1 по EN 13300); категория К3 по СП 71.13330.2017, табл. 7.5; по ГКЛ каркаса П113, влагостойкая окраска; Q3 колеруется в код стен, но по эмали на МДФ: сличать отдельным выкрасом на своей подложке (выкрас № 10); плинтус в цвет: стены
7	Прихожая-коридор 7,80 м²	ГКЛ по каркасу П113, отм. +2,600; окраска, Tikkurila Anti-Reflex 2, глубокоматовая, 2 слоя, подготовка Q3	Tikkurila F497	7,80	Окраска, Tikkurila Optiva 20 Semimatt, полуматовая, 2 слоя, подготовка К3	Tikkurila J484	23,80	Плинтус МДФ h=80 мм, аналог: МДФ под окраску 80×16 мм	Tikkurila J484	8,7	Аналог: керамогранит матовый R10, тон V486, 600×600×10 мм; тип 3, отм. ЧП ±0,000	7,80	Н стен 2600 (до потолка); колеруется в код стен, но по эмали на МДФ: сличать отдельным выкрасом на своей подложке (выкрас № 10); плинтус в цвет: стены
8	Гардеробная 2 1,29 м²	ГКЛ по каркасу П113, отм. +2,600; окраска, Tikkurila Anti-Reflex 2, глубокоматовая, 2 слоя, подготовка Q3	Tikkurila F497	1,29	Окраска, Tikkurila Optiva 5 Matt, матовая, 2 слоя, подготовка К3	Tikkurila F497	8,65	Плинтус МДФ h=80 мм, аналог: МДФ под окраску 80×16 мм	Tikkurila F497	3,3	Инженерная доска, аналог: дуб натуральный брашированный, масло-воск, 14/4 мм, на клею; тип 1, отм. ЧП ±0,000	1,29	Н стен 2600 (до потолка); колеруется в код стен, но по эмали на МДФ: сличать отдельным выкрасом на своей подложке (выкрас № 10); плинтус в цвет: стены
9	Детская 2 10,96 м²	ГКЛ по каркасу П113, отм. +2,600; окраска, Tikkurila Anti-Reflex 2, глубокоматовая, 2 слоя, подготовка Q3	Tikkurila F497	10,96	Окраска, Tikkurila Joker, полуматовая, 2 слоя, подготовка К3	Tikkurila F497	29,08	Плинтус МДФ h=80 мм, аналог: МДФ под окраску 80×16 мм	Tikkurila F497	11,8	Инженерная доска, аналог: дуб натуральный брашированный, масло-воск, 14/4 мм, на клею; тип 1, отм. ЧП ±0,000	10,96	Н стен 2600 (до потолка); колеруется в код стен, но по эмали на МДФ: сличать отдельным выкрасом на своей подложке (выкрас № 10); плинтус в цвет: стены
10	Санузел 1,31 м²	ГКЛВ по каркасу П113, отм. +2,500; окраска, Tikkurila Luja 7, матовая, 2 слоя, подготовка Q3	Tikkurila F497	1,31	Облицовка плиткой, аналог: керамогранит матовый, тон F497, 600×600×9 мм, клей C2 TE S1, затирка CG2WA	#F1F1EC	10,46	нет (облицовка от пола)			Аналог: керамогранит матовый R10, тон J484, 600×600×10 мм; тип 2, отм. ЧП −0,015	1,31	Н стен 2515 (до потолка); тёплый пол; гидроизоляция обмазочная, 2 слоя, по всему помещению, с заведением на стены 200 мм (по пирогу пола); тест проливом и акт скрытых работ; облицовка от чистого пола до низа потолка; по ГКЛВ каркаса П113, влагостойкая окраска; Q3

Примечания

1. Ведомость продолжена на листе 3 из 3; итоги, сводка площадей и примечания — на последнем листе ведомости.

Допущения и предложения на листе

Основа листа: размеры сняты с размерных цепочек растрового скана плана заказчика, на объекте не замерены; ступени наружного контура приведены к граням помещений модели (ИЗ-8, К-20, К-21); высота потолка 2700 мм принята, источника нет (К-24); тип дома и перекрытие (монолит, плита 220 мм) приняты, источника нет (К-3); толщины стен приняты (250 и 120 мм), источника нет (К-21); мощность 15 кВт принята, технических условий нет (К-25).

Знак «**» — предложение проектировщика, заказчиком не утверждено (согласовать с заказчиком): ИЗ-1, К-26: пол пом. 9 — направление паркета изменено вслед за окном: по оси X → по оси Y; артикул изделия не выбран: позиция описана характеристиками («аналог по характеристикам»), артикул выбирается при закупке; К-26: пол пом. 1–8, 10–13, плинтус пом. 1, 3–9, 11–13, акцент пом. 1, 11, стены пом. 2, 10, фартук пом. 6 — артикул изделия не выбран: позиция описана характеристиками («аналог по характеристикам»), артикул выбирается при закупке.

Открытые вопросы и конфликты по листу: К-26.

См. лист открытых вопросов (лист 6, запись К-3; лист 7, записи К-20, К-21, К-24, К-25; лист 8, запись К-26; лист 9, запись ИЗ-1; лист 10, запись ИЗ-8).

Изм.	Кол.уч	Лист	№ док.	Подп.	Дата
Разраб.		Кырлан А.С.			21.10.26
Пров.					
ГИП		Кырлан А.С.			21.10.26
Н. контр.					
Утв.					

ГД-2026-004-АИ

Четырёхкомнатная квартира

Общая площадь 102,67* м² · * размеры со скана, не замерены (реестр — л. 6–11, ИЗ-8, К-20, К-21)

Дизайн-проект интерьера четырёхкомнатной квартиры

Стадия	Лист	Листов
РП	56	124

Ведомость отделки помещений. Лист 2 из 3

М б/м

Кырлан Александр Сергеевич

выпуск 05.10.2026 № 7e7a2cd217 · стр. 65 из 168

Ведомость отделки помещений. Лист 3 из 3

Потолки, стены, низ стен, полы · площади в м², длины в м · отметки в м

Ведомость отделки помещений (форма 1 прил. А ГОСТ 21.501-2018). Лист 3 из 3

№	Наименование помещения	Потолок			Стены и перегородки			Низ стен (плинтус)			Пол		Примечание
		Вид отделки	Код цвета	S, м²	Вид отделки	Код цвета	S, м²	Вид отделки	Код цвета	L, м	Вид отделки	S, м²	
11	Гостиная 14,55 м²	ГКЛ по каркасу П113, отм. +2,500; +2,600; окраска, Tikkurila Anti-Reflex 2, глубокоматовая, 2 слоя, подготовка Q3	Tikkurila F497	14,55	Окраска, Tikkurila Optiva 5 Matt, матовая, 2 слоя, подготовка К3 Акцент — стена А: окраска, Tikkurila Optiva 5 Matt, матовая, 3 слоя, подготовка К3	Tikkurila F497 Tikkurila L481	26,52 10,70	Плинтус МДФ h=80 мм, аналог: МДФ под окраску 80×16 мм	Tikkurila F497	15,6	Инженерная доска, аналог: дуб натуральный брашированный, масло-воск, 14/4 мм, на клею; тип 1, отм. ЧП ±0,000	14,55	Н стен 2500 (до потолка); колеруется в код стен, но по эмали на МДФ: сличать отдельным выкрасом на своей подложке (выкрас № 10); плинтус в цвет: стены
12	Гардеробная 1 2,83 м²	ГКЛ по каркасу П113, отм. +2,600; окраска, Tikkurila Anti-Reflex 2, глубокоматовая, 2 слоя, подготовка Q3	Tikkurila F497	2,83	Окраска, Tikkurila Optiva 5 Matt, матовая, 2 слоя, подготовка К3	Tikkurila F497	14,96	Плинтус МДФ h=80 мм, аналог: МДФ под окраску 80×16 мм	Tikkurila F497	5,5	Инженерная доска, аналог: дуб натуральный брашированный, масло-воск, 14/4 мм, на клею; тип 1, отм. ЧП ±0,000	2,83	Н стен 2600 (до потолка); колеруется в код стен, но по эмали на МДФ: сличать отдельным выкрасом на своей подложке (выкрас № 10); плинтус в цвет: стены
13	Балкон 1 3,70 м²	ГКЛВ по каркасу П113, отм. +2,500; окраска, Tikkurila Luja 7, матовая, 2 слоя, подготовка Q3	Tikkurila F497	3,70	Окраска, Tikkurila Luja 7, полуматовая, 2 слоя, подготовка К3	Tikkurila F497	16,51	Плинтус из керамогранита h=80 мм, аналог: из керамогранита пола, подрезка 80 мм, верхняя кромка с запилом 45°	#B8AFA5	7,7	Аналог: керамогранит матовый R11, тон V486, 600×600×10 мм; тип 5, отм. ЧП −0,030	3,70	Н стен 2530 (до потолка); влагостойкая окраска по утеплённой стене; категория К3 по СП 71.13330.2017, табл. 7.5; по ГКЛВ каркаса П113, влагостойкая окраска; Q3
	Итого			**106,37**			**317,37**			**113,7**		**106,37**	

Сводка площадей по материалам отделки

Поверхность	Материал / код цвета	Серия	Площадь, м²
Потолок	Tikkurila F497	Anti-Reflex 2	80,60
Потолок	Tikkurila F497	Luja 7	25,77
Стены	Tikkurila F497	Optiva 5 Matt	93,00
Стены	Tikkurila L481	Optiva 5 Matt	24,25
Стены	облицовка плиткой 600×600×9 мм, #F1F1EC	аналог: керамогранит матовый, тон F497	32,81
Стены	Tikkurila F497	Joker	69,20
Стены	Tikkurila J484	Optiva 20 Semimatt	46,01
Стены	Tikkurila F497	Luja 7	50,99
Фартук	облицовка керамогранитом 600×600×9 мм, #F1F1EC	аналог: керамогранит матовый, тон F497	1,11

Допущения и предложения на листе

Основа листа: размеры сняты с размерных цепочек растрового скана плана заказчика, на объекте не замерены; ступени наружного контура приведены к граням помещений модели (ИЗ-8, К-20, К-21); высота потолка 2700 мм принята, источника нет (К-24); тип дома и перекрытие (монолит, плита 220 мм) приняты, источника нет (К-3); толщины стен приняты (250 и 120 мм), источника нет (К-21); мощность 15 кВт принята, технических условий нет (К-25).

Знак «**» — предложение проектировщика, заказчиком не утверждено (согласовать с заказчиком): ИЗ-1, К-26: пол пом. 9 — направление паркета изменено вслед за окном: по оси X → по оси Y; артикул изделия не выбран: позиция описана характеристиками («аналог по характеристикам»), артикул выбирается при закупке; К-26: пол пом. 1–8, 10–13, плинтус пом. 1, 3–9, 11–13, акцент пом. 1, 11, стены пом. 2, 10, фартук пом. 6 — артикул изделия не выбран: позиция описана характеристиками («аналог по характеристикам»), артикул выбирается при закупке.

Открытые вопросы и конфликты по листу: К-26.

См. лист открытых вопросов (лист 6, запись К-3; лист 7, записи К-20, К-21, К-24, К-25; лист 8, запись К-26; лист 9, запись ИЗ-1; лист 10, запись ИЗ-8).

Примечания

1. Площади поверхностей — по чистым граням стен до отделки: стены = периметр × высоту от чистого пола помещения до низа потолка минус проёмы (облицовка плиткой — до верха облицовки); плинтус = периметр минус дверные проёмы; пол и потолок — по площади помещения. Количество плиток по раскладке. Площади помещений — с учётом всех частей помещения; откосы в площадь стен не входят.
2. Акцентные стены и фартук — отдельными строками, их площадь вычтена из основной отделки стен помещения; фартук — над нижними модулями кухни от столешницы до низа навесных шкафов, где шкафов нет — на 600 мм.
3. Плинтус — длина по периметру за вычетом дверных проёмов; примыкания к наличникам и встроенной мебели — по развёрткам.
4. Формат плитки — Ш×В×Т (ширина × высота в положении укладки × толщина), мм; на полу — вдоль стен А/В × вдоль стен Б/Г.
5. Коды цвета — по веерам производителей; колеровка каждой краски одной партией, проверка выкраса при свете D65 и при лампах проекта.
6. Уровни подготовки Q1–Q4 — система Knauf, не норма ГОСТ/СП; допуски поверхностей — по СП 71.13330.2017 (действующая редакция).
7. «аналог:» — изделие задано характеристиками, марку и артикул согласовать с заказчиком до закупки.
8. Плавающая стяжка по звукоизоляции: демпферная (кромочная) лента по контуру помещения и у стояков (СП 51.13330.2011, п. 9.11); плинтус крепится только к стене.

Изм.	Кол.уч	Лист	№ док.	Подп.	Дата
Разраб.		Кырлан А.С.			21.10.26
Пров.					
ГИП		Кырлан А.С.			21.10.26
Н. контр.					
Утв.					

ГД-2026-004-АИ

Четырёхкомнатная квартира

Общая площадь 102,67* м² · * размеры со скана, не замерены (реестр — л. 6–11, ИЗ-8, К-20, К-21)

Дизайн-проект интерьера четырёхкомнатной квартиры

Стадия	Лист	Листов
РП	57	124

Ведомость отделки помещений. Лист 3 из 3

М б/м

Кырлан Александр Сергеевич

выпуск 05.10.2026 № 7e7a2cd217 · стр. 66 из 168

Колерная карта

Цвета и материалы по помещениям · палитра проекта · лист 1 из 2

Колерная карта по помещениям

Помещение	Поверхность	Образец	Поз.	Система и код цвета	Производитель, линейка / материал, артикул	Блеск	Класс EN 13300	LRV	Площадь
1. Зал 18,16 м²	стены		**К1**	Tikkurila F497	Tikkurila · Optiva 5 Matt	матовая	2	88	25,9 м²
	акцент А		**К2**	Tikkurila L481	Tikkurila · Optiva 5 Matt	матовая	2	18	13,6 м²
	потолок		**К3**	Tikkurila F497	Tikkurila · Anti-Reflex 2	глубокомат.	2	88	18,2 м²
	пол		**КМ1**	по образцу	инженерная доска · аналог по хар.				18,2 м²
	плинтус		**К4**	Tikkurila F497	МДФ · в цвет Tikkurila	полуглянц.	2	88	16,6 м
2. Ванная комната 5,57 м²	стены		**КМ2**	тон Paper F497 (тёплый белый)	плитка · аналог по хар.				22,3 м²
	потолок		**К5**	Tikkurila F497	Tikkurila · Luja 7	матовая	1	88	5,6 м²
	пол		**КМ3**	тон Castle J484 (тёплый песочный)	керамогранит · аналог по хар.				5,6 м²
3. Тёмная комната 2,96 м²	стены		**К1**	Tikkurila F497	Tikkurila · Optiva 5 Matt	матовая	2	88	16,9 м²
	потолок		**К3**	Tikkurila F497	Tikkurila · Anti-Reflex 2	глубокомат.	2	88	3,0 м²
	пол		**КМ1**	по образцу	инженерная доска · аналог по хар.				3,0 м²
	плинтус		**К4**	Tikkurila F497	МДФ · в цвет Tikkurila	полуглянц.	2	88	6,4 м
4. Детская 1 17,51 м²	стены		**К6**	Tikkurila F497	Tikkurila · Joker	полуматов.	2	88	40,1 м²
	потолок		**К3**	Tikkurila F497	Tikkurila · Anti-Reflex 2	глубокомат.	2	88	17,5 м²
	пол		**КМ1**	по образцу	инженерная доска · аналог по хар.				17,5 м²
	плинтус		**К4**	Tikkurila F497	МДФ · в цвет Tikkurila	полуглянц.	2	88	16,2 м
5. Коридор 4,54 м²	стены		**К7**	Tikkurila J484	Tikkurila · Optiva 20 Semimatt	полуматов.	2	55	22,2 м²
	потолок		**К3**	Tikkurila F497	Tikkurila · Anti-Reflex 2	глубокомат.	2	88	4,5 м²
	пол		**КМ4**	тон Claystone V486 (грейж)	керамогранит · аналог по хар.				4,5 м²
	плинтус		**К8**	Tikkurila J484	МДФ · в цвет Tikkurila	полуглянц.	2	55	8,1 м
6. Кухня 15,19 м²	стены		**К9**	Tikkurila F497	Tikkurila · Luja 7	полуматов.	1	88	34,5 м²
	потолок		**К5**	Tikkurila F497	Tikkurila · Luja 7	матовая	1	88	15,2 м²
	пол		**КМ1**	по образцу	инженерная доска · аналог по хар.				15,2 м²
	плинтус		**К4**	Tikkurila F497	МДФ · в цвет Tikkurila	полуглянц.	2	88	13,8 м
	фартук		**КМ5**	тон Paper F497 (тёплый белый)	керамогранит · аналог по хар.				1,1 м²

Схема палитры проекта

Стиль: Современный (контемпорари) · схема: аналоговая

основной	основной	второстепенный	акцентный
Tikkurila F497	**Tikkurila J484**	**Tikkurila V486**	**Tikkurila L481**
Paper LRV 88 стены 1,3,4,6,8,9,11,12,13; потолок 1,2,3,4,5,6,7,8,9,10,11,12,13; плинтус 1,3,4,6,8,9,11,12; текстиль/декор 1	Castle LRV 55 стены 5,7; плинтус 5,7; текстиль/декор 1,6	Claystone LRV 44 текстиль/декор 1,13	Silhouette LRV 18 акцент 1,11; текстиль/декор 1,11

План 60/30/10

Окраска, факт — по площади стен, акцентов, потолков

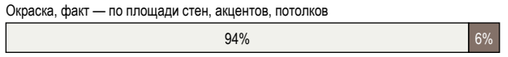

окрашено всего 389,8 м²; второстепенный тон несут мебель и текстиль

Текстиль и декор в цветах вне палитры проекта

- NCS S 3005-Y20R тёплый тауп-серый — пом. 1 (Т3), 7 (Т15), 9 (Т18)
- Tikkurila H487 Pumice — пом. 1 (Т4), 4 (Т9, Т10, Т11), 9 (Т17**, Т19)
- Tikkurila V484 Driftwood — пом. 4 (Т8), 9 (Т16**), 13 (Т23)
- NCS S 5010-B10G серо-петроль — пом. 4 (Т12, Т13)
- Farrow & Ball No. 47 Green Smoke — пом. 9 (Т20, Т21)

Условные обозначения

- **К1** Tikkurila F497 · Paper · Optiva 5 Matt · матовая · кл. 2
- **К2** Tikkurila L481 · Silhouette · Optiva 5 Matt · матовая · кл. 2
- **К3** Tikkurila F497 · Paper · Anti-Reflex 2 · глубокомат. · кл. 2
- **К4** Tikkurila F497 · Paper · МДФ · полуглянц. · кл. 2
- **К5** Tikkurila F497 · Paper · Luja 7 · матовая · кл. 1
- **К6** Tikkurila F497 · Paper · Joker · полуматов. · кл. 2
- **К7** Tikkurila J484 · Castle · Optiva 20 Semimatt · полуматов. · кл. 2
- **К8** Tikkurila J484 · Castle · МДФ · полуглянц. · кл. 2
- **К9** Tikkurila F497 · Paper · Luja 7 · полуматов. · кл. 1
- дерево (доска, паркет, ламинат) — рисунок досок
- керамогранит, плитка, камень — сетка швов по формату

- **КМ1** инженерная доска · аналог: дуб натуральный брашированный, масло-воск, 14/4 мм
- **КМ2** плитка · аналог: керамогранит матовый, тон F497, 600×600×9 мм
- **КМ3** аналог: керамогранит матовый R10, тон J484, 600×600×10 мм
- **КМ4** аналог: керамогранит матовый R10, тон V486, 600×600×10 мм
- **КМ5** аналог: керамогранит матовый, тон F497, 600×600×9 мм
- **КМ6** аналог: керамогранит матовый R11, тон V486, 600×600×10 мм
- **КМ7** керамогранит · аналог: плинтус из керамогранита пола, подрезка 80 мм, верхняя кромка с запилом 45°

К — позиция окраски (код + продукт + блеск), КМ — позиция материала, тон КМ — по описанию артикула, эталон — образец материала; ≈ LRV — расчёт по HEX, справочно

Допущения и предложения на листе

Основа листа: размеры сняты с размерных цепочек растрового скана плана заказчика, на объекте не замерены; ступени наружного контура приведены к граням помещений модели (ИЗ-8, К-20, К-21); высота потолка 2700 мм принята, источника нет (К-24); тип дома и перекрытие (монолит, плита 220 мм) приняты, источника нет (К-3); толщины стен приняты (250 и 120 мм), источника нет (К-21); мощность 15 кВт принята, технических условий нет (К-25).

Знак «**» — предложение проектировщика, заказчиком не утверждено (согласовать с заказчиком): ИЗ-1: Т16, Т17; ИЗ-1, К-26: пол пом. 9 — направление паркета изменено вслед за окном: по оси X → по оси Y; артикул изделия не выбран: позиция описана характеристиками («аналог по характеристикам»), артикул выбирается при закупке; К-26: пол пом. 1–8, 10–13, плинтус пом. 1, 3–9, 11–13, акцент пом. 1, 11, стены пом. 2, 10, фартук пом. 6 — артикул изделия не выбран: позиция описана характеристиками («аналог по характеристикам»), артикул выбирается при закупке.

Открытые вопросы и конфликты по листу: К-7, К-17, К-26.

Изменения по листу без подписи: ИЗ-7, ИЗ-11.

См. лист открытых вопросов (лист 6, записи К-3, К-7; лист 7, записи К-17, К-20, К-21, К-24, К-25; лист 8, запись К-26; лист 9, записи ИЗ-1, ИЗ-7; лист 10, записи ИЗ-8, ИЗ-11).

Примечания

1. Цвет утверждается только по выкрасу на объекте: формат от А3 до 1000×1000 мм на загрунтованном ГКЛ, в 2 слоя (как на стене), не на белой шпаклёвке; смотреть днём и при свете проекта своего помещения, рядом с образцами пола и фасадов. Подпись на обороте: код, бренд и веер, дата.
2. Колеровка машинная в колеровочном центре бренда; каждый код — за один проход, одной партией на весь объём. Колеровщику передаётся только система и код утверждённого веера; плашки и HEX на листе — ориентир, печать не является эталоном цвета.
3. Класс мокрого истирания — EN 13300 (ISO 11998); блеск — по ГОСТ 31975 (ISO 2813), геометрия 60°. LRV — пересчёт координаты L* каталога производителя (Y = ((L*+16)/116)³); «≈» — расчёт по HEX, справочно.
4. Площади поверхностей — тем же способом и с теми же цифрами, что в ведомости отделки (способ счёта — в общих указаниях); объём краски к заказу, фасовка и материалы КМ — в спецификации отделочных материалов.
5. Колерная карта на 2 листах: обозначения повторены на каждом, схема квартиры и палитра — на первом, перечень выкрасов — на последнем.

Изм.	Кол.уч	Лист	№ док.	Подп.	Дата
Разраб.		Кырлан А.С.			21.10.26
Пров.					
ГИП		Кырлан А.С.			21.10.26
Н. контр.					
Утв.					

ГД-2026-004-АИ

Четырёхкомнатная квартира

Общая площадь 102,67* м² · * размеры со скана, не замерены (реестр — л. 6–11, ИЗ-8, К-20, К-21)

Дизайн-проект интерьера четырёхкомнатной квартиры

Стадия	Лист	Листов
РП	58	124

Колерная карта

М б/м

Кырлан Александр Сергеевич

выпуск 05.10.2026 № 7e7a2cd217 · стр. 67 из 168

Колерная карта

Цвета и материалы по помещениям · выкрасы на согласование · лист 2 из 2

Колерная карта по помещениям (продолжение)

Помещение	Поверхность	Образец	Поз.	Система и код цвета	Производитель, линейка / материал, артикул	Блеск	Класс EN 13300	LRV	Площадь
7. Прихожая-коридор 7,8 м²	стены		**К7**	Tikkurila J484	Tikkurila · Optiva 20 Semimatt	полуматов.	2	55	23,8 м²
	потолок		**К3**	Tikkurila F497	Tikkurila · Anti-Reflex 2	глубокомат.	2	88	7,8 м²
	пол		**КМ4**	тон Claystone V486 (грейж)	керамогранит · аналог по хар.				7,8 м²
	плинтус		**К8**	Tikkurila J484	МДФ · в цвет Tikkurila	полуглянц.	2	55	8,7 м
8. Гардеробная 2 1,29 м²	стены		**К1**	Tikkurila F497	Tikkurila · Optiva 5 Matt	матовая	2	88	8,7 м²
	потолок		**К3**	Tikkurila F497	Tikkurila · Anti-Reflex 2	глубокомат.	2	88	1,3 м²
	пол		**КМ1**	по образцу	инженерная доска · аналог по хар.				1,3 м²
	плинтус		**К4**	Tikkurila F497	МДФ · в цвет Tikkurila	полуглянц.	2	88	3,3 м
9. Детская 2 10,96 м²	стены		**К6**	Tikkurila F497	Tikkurila · Joker	полуматов.	2	88	29,1 м²
	потолок		**К3**	Tikkurila F497	Tikkurila · Anti-Reflex 2	глубокомат.	2	88	11,0 м²
	пол		**КМ1**	по образцу	инженерная доска · аналог по хар.				11,0 м²
	плинтус		**К4**	Tikkurila F497	МДФ · в цвет Tikkurila	полуглянц.	2	88	11,8 м
10. Санузел 1,31 м²	стены		**КМ2**	тон Paper F497 (тёплый белый)	плитка · аналог по хар.				10,5 м²
	потолок		**К5**	Tikkurila F497	Tikkurila · Luja 7	матовая	1	88	1,3 м²
	пол		**КМ3**	тон Castle J484 (тёплый песочный)	керамогранит · аналог по хар.				1,3 м²
11. Гостиная 14,55 м²	стены		**К1**	Tikkurila F497	Tikkurila · Optiva 5 Matt	матовая	2	88	26,5 м²
	акцент А		**К2**	Tikkurila L481	Tikkurila · Optiva 5 Matt	матовая	2	18	10,7 м²
	потолок		**К3**	Tikkurila F497	Tikkurila · Anti-Reflex 2	глубокомат.	2	88	14,6 м²
	пол		**КМ1**	по образцу	инженерная доска · аналог по хар.				14,6 м²
	плинтус		**К4**	Tikkurila F497	МДФ · в цвет Tikkurila	полуглянц.	2	88	15,6 м
12. Гардеробная 1 2,83 м²	стены		**К1**	Tikkurila F497	Tikkurila · Optiva 5 Matt	матовая	2	88	15,0 м²
	потолок		**К3**	Tikkurila F497	Tikkurila · Anti-Reflex 2	глубокомат.	2	88	2,8 м²
	пол		**КМ1**	по образцу	инженерная доска · аналог по хар.				2,8 м²
	плинтус		**К4**	Tikkurila F497	МДФ · в цвет Tikkurila	полуглянц.	2	88	5,5 м
13. Балкон 1 3,7 м²	стены		**К9**	Tikkurila F497	Tikkurila · Luja 7	полуматов.	1	88	16,5 м²
	потолок		**К5**	Tikkurila F497	Tikkurila · Luja 7	матовая	1	88	3,7 м²
	пол		**КМ6**	тон Claystone V486 (грейж)	керамогранит · аналог по хар.				3,7 м²
	плинтус		**КМ7**	тон Claystone V486 (грейж)	керамогранит · аналог по хар.				7,7 м

Условные обозначения

- **К1** — Tikkurila F497 · Paper · Optiva 5 Matt · матовая · кл. 2
- **К2** — Tikkurila L481 · Silhouette · Optiva 5 Matt · матовая · кл. 2
- **К3** — Tikkurila F497 · Paper · Anti-Reflex 2 · глубокомат. · кл. 2
- **К4** — Tikkurila F497 · Paper · МДФ · полуглянц. · кл. 2
- **К5** — Tikkurila F497 · Paper · Luja 7 · матовая · кл. 1
- **К6** — Tikkurila F497 · Paper · Joker · полуматов. · кл. 2
- **К7** — Tikkurila J484 · Castle · Optiva 20 Semimatt · полуматов. · кл. 2
- **К8** — Tikkurila J484 · Castle · МДФ · полуглянц. · кл. 2
- **К9** — Tikkurila F497 · Paper · Luja 7 · полуматов. · кл. 1
- дерево (доска, паркет, ламинат) — рисунок досок
- керамогранит, плитка, камень — сетка швов по формату

- **КМ1** — инженерная доска · аналог: дуб натуральный брашированный, масло-воск, 14/4 мм
- **КМ2** — плитка · аналог: керамогранит матовый, тон F497, 600×600×9 мм
- **КМ3** — аналог: керамогранит матовый R10, тон J484, 600×600×10 мм
- **КМ4** — аналог: керамогранит матовый R10, тон V486, 600×600×10 мм
- **КМ5** — аналог: керамогранит матовый, тон F497, 600×600×9 мм
- **КМ6** — аналог: керамогранит матовый R11, тон V486, 600×600×10 мм
- **КМ7** — керамогранит · аналог: плинтус из керамогранита пола, подрезка 80 мм, верхняя кромка с запилом 45°

К — позиция окраски (код + продукт + блеск), КМ — позиция материала, тон КМ — по описанию артикула, эталон — образец материала; ≈ LRV — расчёт по HEX, справочно

Допущения и предложения на листе

Основа листа: размеры сняты с размерных цепочек растрового скана плана заказчика, на объекте не замерены; ступени наружного контура приведены к граням помещений модели (ИЗ-8, К-20, К-21); высота потолка 2700 мм принята, источника нет (К-24); тип дома и перекрытие (монолит, плита 220 мм) приняты, источника нет (К-3); толщины стен приняты (250 и 120 мм), источника нет (К-21); мощность 15 кВт принята, технических условий нет (К-25).

Знак «**» — предложение проектировщика, заказчиком не утверждено (согласовать с заказчиком): ИЗ-1, К-26: пол пом. 9 — направление паркета изменено вслед за окном: по оси X → по оси Y; артикул изделия не выбран: позиция описана характеристиками («аналог по характеристикам»), артикул выбирается при закупке; К-26: пол пом. 1–8, 10–13, плинтус пом. 1, 3–9, 11–13, акцент пом. 1, 11, стены пом. 2, 10, фартук пом. 6 — артикул изделия не выбран: позиция описана характеристиками («аналог по характеристикам»), артикул выбирается при закупке.

Открытые вопросы и конфликты по листу: К-7, К-17, К-26.

Изменения по листу без подписи: ИЗ-7, ИЗ-11.

См. лист открытых вопросов (лист 6, записи К-3, К-7; лист 7, записи К-17, К-20, К-21, К-24, К-25; лист 8, запись К-26; лист 9, записи ИЗ-1, ИЗ-7; лист 10, записи ИЗ-8, ИЗ-11).

Перечень выкрасов на согласование

№	Код	Бренд / веер	Пом. / стена	Подложка	Формат	Статус
1	F497	Tikkurila Symphony / Feel the Colour	1	ГКЛ, загрунтованный под эту краску	600×1000	на согласов.
2	G503	Tikkurila Symphony / Feel the Colour	1	ГКЛ, загрунтованный под эту краску	600×1000	на согласов.
3	G497	Tikkurila Symphony / Feel the Colour	1	ГКЛ, загрунтованный под эту краску	600×1000	на согласов.
4	L481	Tikkurila Symphony / Feel the Colour	1 А	ГКЛ, загрунтованный под эту краску	600×1000	на согласов.
5	V477	Tikkurila Symphony / Feel the Colour	1 А	ГКЛ, загрунтованный под эту краску	600×1000	на согласов.
6	L462	Tikkurila Symphony / Feel the Colour	1 А	ГКЛ, загрунтованный под эту краску	600×1000	на согласов.
7	J484	Tikkurila Symphony / Feel the Colour	5	ГКЛ, загрунтованный под эту краску	600×1000	на согласов.
8	X487	Tikkurila Symphony / Feel the Colour	5	ГКЛ, загрунтованный под эту краску	600×1000	на согласов.
9	X463	Tikkurila Symphony / Feel the Colour	5	ГКЛ, загрунтованный под эту краску	600×1000	на согласов.

… ещё 2 выкрасов — в ведомости отделки

Примечания

1. Цвет утверждается только по выкрасу на объекте: формат от А3 до 1000×1000 мм на загрунтованном ГКЛ, в 2 слоя (как на стене), не на белой шпаклёвке; смотреть днём и при свете проекта своего помещения, рядом с образцами пола и фасадов. Подпись на обороте: код, бренд и веер, дата.
2. Колеровка машинная в колеровочном центре бренда; каждый код — за один проход, одной партией на весь объём. Колеровщику передаётся только система и код утверждённого веера; плашки и HEX на листе — ориентир, печать не является эталоном цвета.
3. Класс мокрого истирания — EN 13300 (ISO 11998); блеск — по ГОСТ 31975 (ISO 2813), геометрия 60°. LRV — пересчёт координаты L* каталога производителя (Y = ((L*+16)/116)³); «≈» — расчёт по HEX, справочно.
4. Площади поверхностей — тем же способом и с теми же цифрами, что в ведомости отделки (способ счёта — в общих указаниях); объём краски к заказу, фасовка и материалы КМ — в спецификации отделочных материалов.
5. Колерная карта на 2 листах: обозначения повторены на каждом, схема квартиры и палитра — на первом, перечень выкрасов — на последнем.

Изм.	Кол.уч	Лист	№ док.	Подп.	Дата
Разраб.		Кырлан А.С.			21.10.26
Пров.					
ГИП		Кырлан А.С.			21.10.26
Н. контр.					
Утв.					

ГД-2026-004-АИ

Четырёхкомнатная квартира

Общая площадь 102,67* м² · * размеры со скана, не замерены (реестр — л. 6–11, ИЗ-8, К-20, К-21)

Дизайн-проект интерьера четырёхкомнатной квартиры

Стадия	Лист	Листов
РП	59	124

Колерная карта

М б/м

Кырлан Александр Сергеевич

выпуск 05.10.2026 № 7e7a2cd217 · стр. 68 из 168

Спецификация отделочных материалов

ПРЕДВАРИТЕЛЬНО · не для производства работ · открыто пунктов: 30 (реестр — л. 6–11)

Форма 1 по ГОСТ 21.110-2013 · количества — из геометрии проекта, с запасом · часть 1 из 2

Поз.	Наименование и техническая характеристика	Тип, марка, обозначение документа	Код продукции	Поставщик	Ед. изм.	Кол.	Масса 1 ед., кг	Примечание
	Лакокрасочные материалы							
1	Краска интерьерная водно-дисперсионная акриловая для стен, матовая, класс мокрого истирания 2 по EN 13300, база A; цвет Tikkurila F497 «Paper», колеровка машинная	Tikkurila Optiva 5 Matt		Tikkurila	л	25,2		поз. К1 колерной карты; пом. 1, 3, 8, 11, 12; S = 93,0 м² × 2 сл. × 0,12 л/м² = 22,3 л, +10 % и 0,5 л на подкраску → ≥ 25,1 л; тара 2 × 9 л + 2 × 2,7 л + 2 × 0,9 л
2	Краска интерьерная водно-дисперсионная акриловая для акцентных стен, матовая, класс мокрого истирания 2 по EN 13300, база C; цвет Tikkurila L481 «Silhouette», колеровка машинная	Tikkurila Optiva 5 Matt		Tikkurila	л	10,8		поз. К2 колерной карты; пом. 1, 11; S = 24,3 м² × 3 сл. × 0,12 л/м² = 8,7 л, +10 % и 0,5 л на подкраску → ≥ 10,1 л; тара 1 × 9 л + 2 × 0,9 л
3	Краска интерьерная водно-дисперсионная акриловая для потолков, глубокоматовая, класс мокрого истирания 2 по EN 13300, база A; цвет Tikkurila F497 «Paper», колеровка машинная	Tikkurila Anti-Reflex 2		Tikkurila	л	22,5		поз. К3 колерной карты; пом. 1, 3, 4, 5, 7, 8, 9, 11, 12; S = 80,6 м² × 2 сл. × 0,12 л/м² = 19,3 л, +10 % и 0,5 л на подкраску → ≥ 21,8 л; тара 2 × 9 л + 1 × 2,7 л + 2 × 0,9 л
4	Краска интерьерная водно-дисперсионная акриловая для потолков, матовая, класс мокрого истирания 1 по EN 13300, база A; цвет Tikkurila F497 «Paper», колеровка машинная	Tikkurila Luja 7		Tikkurila	л	8,1		поз. К5 колерной карты; пом. 2, 6, 10, 13; S = 25,8 м² × 2 сл. × 0,12 л/м² = 6,2 л, +10 % и 0,5 л на подкраску → ≥ 7,3 л; тара 3 × 2,7 л
5	Краска интерьерная водно-дисперсионная акриловая для стен, полуматовая, класс мокрого истирания 2 по EN 13300, база A; цвет Tikkurila F497 «Paper», колеровка машинная	Tikkurila Joker		Tikkurila	л	18,9		поз. К6 колерной карты; пом. 4, 9; S = 69,2 м² × 2 сл. × 0,12 л/м² = 16,6 л, +10 % и 0,5 л на подкраску → ≥ 18,8 л; тара 2 × 9 л + 1 × 0,9 л
6	Краска интерьерная водно-дисперсионная акриловая для стен, полуматовая, класс мокрого истирания 2 по EN 13300, база A; цвет Tikkurila J484 «Castle», колеровка машинная	Tikkurila Optiva 20 Semimatt		Tikkurila	л	13,5		поз. К7 колерной карты; пом. 5, 7; S = 46,0 м² × 2 сл. × 0,12 л/м² = 11,0 л, +10 % и 0,5 л на подкраску → ≥ 12,6 л; тара 1 × 9 л + 1 × 2,7 л + 2 × 0,9 л
7	Краска интерьерная водно-дисперсионная акриловая для стен, полуматовая, класс мокрого истирания 1 по EN 13300, база A; цвет Tikkurila F497 «Paper», колеровка машинная	Tikkurila Luja 7		Tikkurila	л	14,4		поз. К9 колерной карты; пом. 6, 13; S = 51,0 м² × 2 сл. × 0,12 л/м² = 12,2 л, +10 % и 0,5 л на подкраску → ≥ 14,0 л; тара 1 × 9 л + 2 × 2,7 л
8	Акрилово-уретановая эмаль на водной основе, полуглянцевая в цвет Tikkurila F497 «Paper» — окраска плинтуса	аналог по характеристикам			л	2,3		поз. К4; пом. 1, 3, 4, 6, 8, 9, 11, 12; L = 89,2 м, S = 8,6 м² × 2 сл. × 0,12 л/м² + 10 %; продукт подобрать в веере Tikkurila
9	Акрилово-уретановая эмаль на водной основе, полуглянцевая в цвет Tikkurila J484 «Castle» — окраска плинтуса	аналог по характеристикам			л	0,5		поз. К8; пом. 5, 7; L = 16,8 м, S = 1,6 м² × 2 сл. × 0,12 л/м² + 10 %; продукт подобрать в веере Tikkurila
10	Грунтовка акриловая под окраску стен и потолков — из системы производителя краски	по системе краски			м²	390		площадь окраски стен, акцентов и потолков; 1 слой перед окраской; расход — по ТУ грунтовки

Допущения и предложения на листе

Основа листа: размеры сняты с размерных цепочек растрового скана плана заказчика, на объекте не замерены; ступени наружного контура приведены к граням помещений модели (ИЗ-8, К-20, К-21); высота потолка 2700 мм принята, источника нет (К-24); тип дома и перекрытие (монолит, плита 220 мм) приняты, источника нет (К-3); толщины стен приняты (250 и 120 мм), источника нет (К-21); мощность 15 кВт принята, технических условий нет (К-25).

Знак «**» — предложение проектировщика, заказчиком не утверждено (согласовать с заказчиком): ИЗ-1, К-26: пол пом. 9 — направление паркета изменено вслед за окном: по оси X → по оси Y; артикул изделия не выбран: позиция описана характеристиками («аналог по характеристикам»), артикул выбирается при закупке; К-26: пол пом. 1–8, 10–13, плинтус пом. 1, 3–9, 11–13, акцент пом. 1, 11, стены пом. 2, 10, фартук пом. 6 — артикул изделия не выбран: позиция описана характеристиками («аналог по характеристикам»), артикул выбирается при закупке.

Открытые вопросы и конфликты по листу: К-26.

См. лист открытых вопросов (лист 6, запись К-3; лист 7, записи К-20, К-21, К-24, К-25; лист 8, запись К-26; лист 9, запись ИЗ-1; лист 10, запись ИЗ-8).

Изм.	Кол.уч	Лист	№ док.	Подп.	Дата
Разраб.		Кырлан А.С.			21.10.26
Пров.					
ГИП		Кырлан А.С.			21.10.26
Н. контр.					
Утв.					

ГД-2026-004-АИ

Четырёхкомнатная квартира

Общая площадь 102,67* м² · * размеры со скана, не замерены (реестр — л. 6–11, ИЗ-8, К-20, К-21)

Дизайн-проект интерьера четырёхкомнатной квартиры

Стадия	Лист	Листов
РП	60	124

Спецификация отделочных материалов

М б/м

Кырлан Александр Сергеевич

выпуск 05.10.2026 № 7e7a2cd217 · стр. 69 из 168

Спецификация отделочных материалов

ПРЕДВАРИТЕЛЬНО · не для производства работ · открыто пунктов: 30 (реестр — л. 6–11)

Форма 1 по ГОСТ 21.110-2013 · количества — из геометрии проекта, с запасом · часть 2 из 2

Поз.	Наименование и техническая характеристика	Тип, марка, обозначение документа	Код продукции	Поставщик	Ед. изм.	Кол.	Масса 1 ед., кг	Примечание
	Плитка и керамогранит							
11	Керамогранит матовый R10, тон J484, 600.8×600.8 мм	аналог по характеристикам			м²	10,47		шов 2 мм; Ванная комната, пол; Санузел, пол; по раскладке 26 шт (S = 6,88 м²), с запасом 29 шт
12	Керамогранит матовый, тон F497, 600.8×600.8 мм	аналог по характеристикам			м²	63,17		шов 2 мм; Ванная комната, стены А–Г; Ванная комната, короб инсталляции; Санузел, стены А–Г; Санузел, короб инсталляции; по раскладке 157 шт (S = 34,22 м²), с запасом 175 шт
13	Керамогранит матовый R10, тон V486, 600.8×600.8 мм	аналог по характеристикам			м²	15,88		шов 2 мм; Коридор, пол; Прихожая-коридор, пол; по раскладке 39 шт (S = 12,34 м²), с запасом 44 шт
14	Керамогранит матовый, тон F497, 600.8×600.8 мм	аналог по характеристикам			м²	1,80		шов 2 мм; Кухня, фартук (ст. А); по раскладке 4 шт (S = 1,11 м²), с запасом 5 шт
15	Керамогранит матовый R11, тон V486, водопоглощение 0,5 % (BIa), противоскольжение R11, PEI IV	аналог по характеристикам			м²	4,07		13. Балкон 1, пол; раскладка не выполнена — S = 3,70 м² + 10 %; клей и затирка — по раскладке
16	Плинтус из керамогранита пола, подрезка 80 мм, верхняя кромка с запилом 45°	аналог по характеристикам			м²	8,46		13. Балкон 1, стены; раскладка не выполнена — S = 7,69 м² + 10 %; клей и затирка — по раскладке
	Напольные покрытия							
17	Дуб натуральный брашированный, масло-воск, 14/4 мм, эмиссия E1, укладка на клей	аналог по характеристикам			м²	89,3		пом. 1, 3, 4, 6, 8, 9, 11, 12; S = 83,45 м² + 7 % (прямая укладка); к заказу — кратно упаковке
18	Клей для паркета и инженерной доски, эластичный (СМП / полиуретановый)	по рекомендации производителя доски			м²	84		площадь приклейки; расход и шпатель — по ТУ клея
	Погонажные изделия							
19	Плинтус МДФ под окраску 80×16 мм, крепление к стене, окраска в цвет Tikkurila F497	аналог по характеристикам			м	117		пом. 1, 3, 4, 5, 6, 7, 8, 9, 11, 12; L = 106,0 м (периметр без дверных проёмов) + 10 % на подрезку; в штуках — по длине планки
20	Плинтус из керамогранита пола, подрезка 80 мм, верхняя кромка с запилом 45°, h = 80 мм, крепление к стене	аналог по характеристикам			м	9		пом. 13; L = 7,7 м (периметр без дверных проёмов) + 10 % на подрезку; в штуках — по длине планки
	Смеси и материалы для облицовки							
21	Затирка для швов плитки, класс CG2WA по EN 13888	аналог: Mapei Ultracolor 133		аналог:	кг	5,7		по раскладке (a+b)/(a·b) × шов × t × 1,6 + 10 %; в т. ч. 0,1 кг — позиции раскладки без марки
22	Клей плиточный C2 TE S1 по EN 12004, слой 5 мм	аналог: Litokol K80 Eco		аналог:	кг	434		18 меш. по 25 кг; 1,5 кг/м² на 1 мм слоя + 10 %; в т. ч. 10 кг — позиции раскладки без марки
23	Гидроизоляция обмазочная мокрых зон: пол, стены по периметру, зоны замачивания; 2 слоя с армирующей лентой в углах	аналог по характеристикам			м²	16,2		площадь по листу раскладки плитки + 10 %; расход смеси — по ТУ
24	Лента демпферная по периметру пола из плитки	аналог по характеристикам			м	29,1		периметр без дверных проёмов + 10 %

Примечания

1. Количества — из геометрии проекта: площади поверхностей по чистым граням стен до отделки (те же, что в ведомости отделки и колерной карте), плитка, клей и затирка — по раскладке плиточника; в графе «Кол.» — к заказу, с запасом.
2. Краска: расход 0,12 л/м² на слой в 2 слоя, если по ТУ не задан иной; запас 10 % и 0,5 л на подкраску каждого кода. Один код — одна партия, колеровка машинная в колеровочном центре бренда; в заказ — только после утверждения выкраса (колерная карта). Фасовка — по каталогу бренда на дату выпуска; к заказу — не меньше расчётного объёма.
3. «Аналог по характеристикам» — допускается изделие другого производителя с характеристиками не ниже указанных, по согласованию с автором проекта.
4. Графы «Код продукции» и «Масса 1 ед.» не заполнены: коды по классификатору продукции не присвоены, масса единицы до 25 кг (ГОСТ 21.110-2013).
5. Грунтовка и клей для доски указаны площадью обработки; объём — по ТУ выбранного продукта.

Допущения и предложения на листе

Основа листа: размеры сняты с размерных цепочек растрового скана плана заказчика, на объекте не замерены; ступени наружного контура приведены к граням помещений модели (ИЗ-8, К-20, К-21); высота потолка 2700 мм принята, источника нет (К-24); тип дома и перекрытие (монолит, плита 220 мм) приняты, источника нет (К-3); толщины стен приняты (250 и 120 мм), источника нет (К-21); мощность 15 кВт принята, технических условий нет (К-25).

Знак «**» — предложение проектировщика, заказчиком не утверждено (согласовать с заказчиком): ИЗ-1, К-26: пол пом. 9 — направление паркета изменено вслед за окном: по оси X → по оси Y; артикул изделия не выбран: позиция описана характеристиками («аналог по характеристикам»), артикул выбирается при закупке; К-26: пол пом. 1–8, 10–13, плинтус пом. 1, 3–9, 11–13, акцент пом. 1, 11, стены пом. 2, 10, фартук пом. 6 — артикул изделия не выбран: позиция описана характеристиками («аналог по характеристикам»), артикул выбирается при закупке.

Открытые вопросы и конфликты по листу: К-26.

См. лист открытых вопросов (лист 6, запись К-3; лист 7, записи К-20, К-21, К-24, К-25; лист 8, запись К-26; лист 9, запись ИЗ-1; лист 10, запись ИЗ-8).

Изм.	Кол.уч	Лист	№ док.	Подп.	Дата
Разраб.		Кырлан А.С.			21.10.26
Пров.					
ГИП		Кырлан А.С.			21.10.26
Н. контр.					
Утв.					

ГД-2026-004-АИ

Четырёхкомнатная квартира

Общая площадь 102,67* м² · * размеры со скана, не замерены (реестр — л. 6–11, ИЗ-8, К-20, К-21)

Дизайн-проект интерьера четырёхкомнатной квартиры

Стадия	Лист	Листов
РП	61	124

Спецификация отделочных материалов

М б/м

Кырлан Александр Сергеевич

Концепция декора и визуализации

Современный (контемпорари) · 13 помещений · визуализации, палитра, материалы, ключевые предметы

Визуализация 1. Вид сверху (3D): планировка с мебелью, текстилем и декором

Расстановка — по плану мебели (лист 24); шторы, ковры, картины и растения — по плану текстиля и декора (лист 63).

Визуализация 22. Зал (пом. 1)

шторы Т1, Т2 · ковёр Т3 · картина ДК1 · зеркало ДК2 · растение ДК3 · подушки, пледы Т4, Т5, Т6, Т7

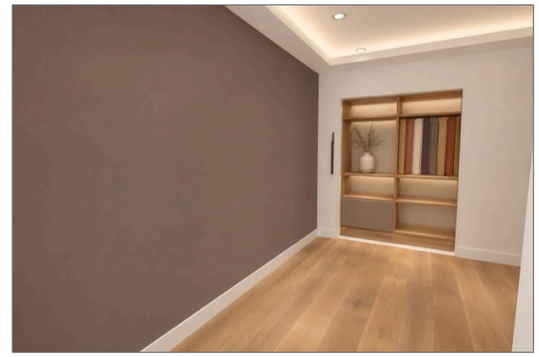

Визуализация 26. Гостиная (пом. 11)

картина ДК20**

Визуализация 21. Кухня (пом. 6)

шторы Т14 · растение ДК9

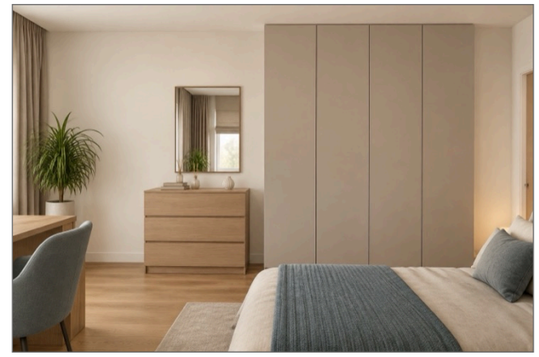

Визуализация 17. Детская 1 (пом. 4)

шторы Т8, Т9 · ковёр Т10 · картина ДК5 · зеркало ДК6 · растение ДК7 · подушки, пледы Т11, Т12, Т13

Материалы и фактуры

Дуб натуральный

пол: пом. 1, 3, 4, 6, 8, 9, 11, 12

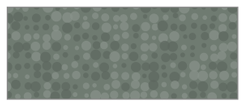

Букле

подушки: Т20

Лён

портьеры, подушки, скатерть: Т1, Т4, Т7, Т8, Т9, Т11, Т14, Т16**,

Бронза и чёрный металл

фурнитура, светильники — бронза

Бархат

подушки: Т5, Т12

Ключевые предметы

— Диван М2 2000×950 — зал; подушки и плед Т4, Т5, Т6

— Кровати М11, М34 — над изголовьем картины ДК5, ДК12; текстиль Т11, Т12, Т13, Т19, Т20, Т21

— Ковры Т3, Т10, Т15, Т18 — шерсть, на противоскользящей подложке

— Картины ДК1, ДК5, ДК12, ДК13, ДК14, ДК15, ДК20** — центр на высоте 1450–1650 мм

— Зеркала в рост ДК18; над умывальниками ДК2, ДК4, ДК6, ДК10, ДК17

— Шторы-волна Т1, Т8, Т16** (Tikkurila V486), тюль Т2 (Tikkurila F497) — в нишах потолка

— Растение ДК3, растение ДК7, растение ДК9, растение ДК11, растение ДК16**, ваза ДК21**, растение ДК19

Настроение

60 % — тёплый белый Paper F497 и песочный Castle J484, 30 % — грейж Claystone V486 в фасадах встроенного хранения и текстиле, 10 % — коричнево-лиловый Silhouette L481 из палитры стиля: ТВ-стена зала, изголовья детских, фасад кухонного острова. По практике тёплая аналоговая гамма ровнее держит цвет в квартире с окнами на разные стороны. Настроение стиля: актуальность, комфорт, мягкая геометрия, контраст фактур, открытость, уверенность. Свет тёплый, 2700–3000 K.

Примечания

1. Визуализации — образ интерьера. Изделия, размеры, высоты подвеса и привязки — по чертежам (план текстиля и декора — лист 63; шторы и карнизы — лист 64; ведомость текстиля — лист 65; ведомость декора и развеска — лист 66); при расхождении действуют чертежи и ведомости.
2. Коды цвета — ориентир подбора по веерам производителей; ткань утверждается по образцу при дневном свете и при свете проекта 2700–3000 K.
3. Мелкий стайлинг на визуализациях (книги, посуда, свечи) в ведомости не входит и поставляется заказчиком по желанию.

Палитра 60/30/10 и цвета текстиля

- Tikkurila F497 (Paper), LRV 88 — 60 % база — Т2
- Tikkurila V486 (Claystone), LRV 44 — 30 % второй цвет — Т1, Т22
- NCS S 3005-Y20R (тёплый тауп-серый), LRV 44 — текстиль — Т3, Т15, Т18
- Tikkurila V484 (Driftwood), LRV 49 — текстиль — Т8, Т16, Т23
- Farrow & Ball No. 47 (Green Smoke), LRV 19 — акцент текстиля — Т20, Т21
- Tikkurila J484 (Castle), LRV 55 — 60 % база — Т7, Т14
- Tikkurila L481 (Silhouette), LRV 18 — 10 % акцент — Т5, Т6
- Tikkurila H487 (Pumice), LRV 57 — текстиль — Т4, Т9, Т10, Т11, Т17, Т19
- NCS S 5010-B10G (серо-петроль), LRV 20 — акцент текстиля — Т12, Т13

Допущения и предложения на листе. Основа листа: размеры сняты с размерных цепочек растрового скана плана заказчика, на объекте не замерены; ступени наружного контура приведены к граням помещений модели (ИЗ-8, К-20, К-21); высота потолка 2700 мм принята, источника нет (К-24); тип дома и перекрытие (монолит, плита 220 мм) приняты, источника нет (К-3); толщины стен приняты (250 и 120 мм), источника нет (К-21); мощность 15 кВт принята, технических условий нет (К-25). Знак «**» — предложение проектировщика, заказчиком не утверждено (согласовать с заказчиком): ИЗ-1: ДК16 — место перенесено (9900; 6100) → (10200; 4300), основание в данных не записано. См. лист открытых вопросов (лист 6, запись К-3; лист 7, записи К-20, К-21, К-24, К-25; лист 9, записи ИЗ-1, ИЗ-7; лист 10, запись ИЗ-8).

						ГД-2026-004-АИ	
						Четырёхкомнатная квартира	
						Общая площадь 102,67* м² · * размеры со скана, не замерены (реестр — л. 6–11, ИЗ-8, К-20, К-21)	
Изм.	Кол.уч	Лист	№ док.	Подп.	Дата	Дизайн-проект интерьера четырёхкомнатной квартиры	Стадия: РП; Лист: 62; Листов: 124
Разраб.		Кырлан А.С.			21.10.26		
Пров.							
ГИП		Кырлан А.С.			21.10.26		
						Концепция декора и визуализации М б/м	**Кырлан Александр Сергеевич**
Н. контр.							
Утв.							

выпуск 05.10.2026 № 7e7a2cd217 · стр. 71 из 168

План текстиля и декора

Шторы и карнизы, ковры, картины и зеркала, растения · размеры в мм от чистовых стен и чистого пола · марки — по ведомостям

ПРЕДВАРИТЕЛЬНО · не для производства работ · открыто пунктов: 30 (реестр — л. 6–11)

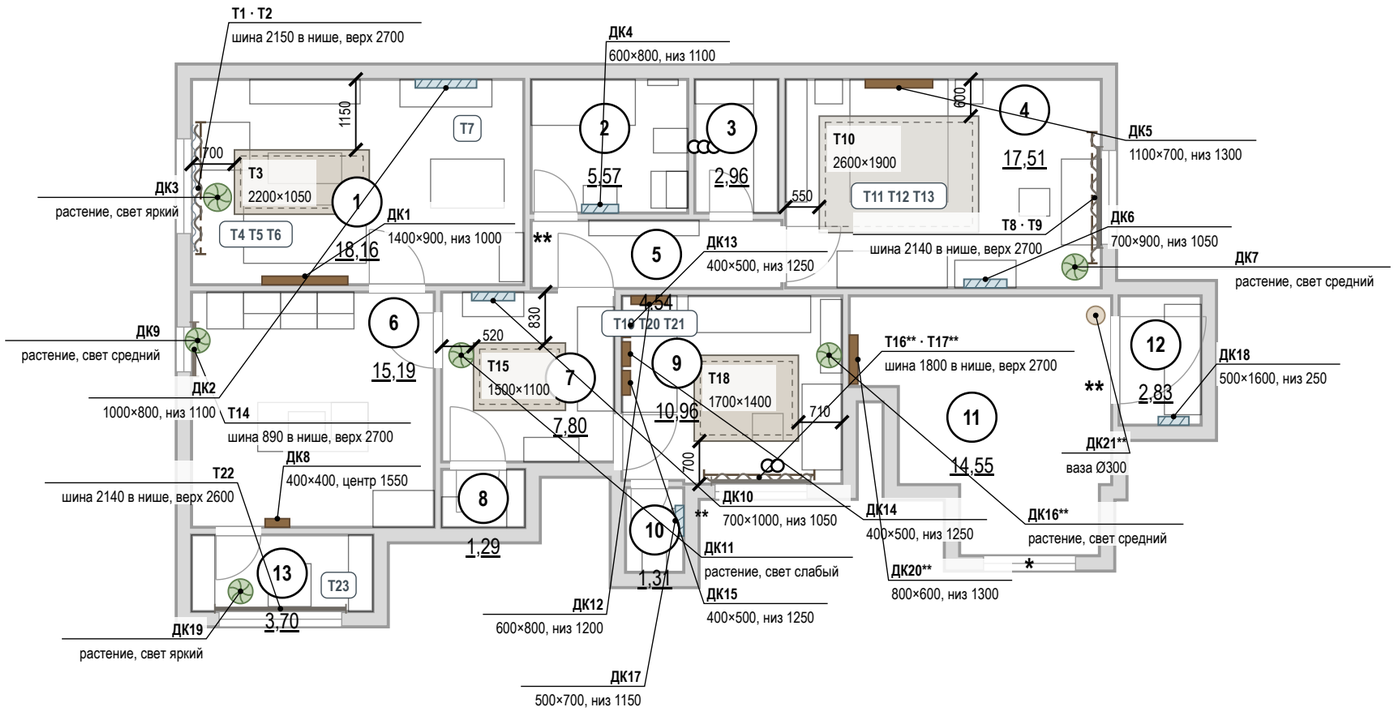

Условные обозначения

- ковёр — габарит в масштабе, цвет изделия
- шина или карниз штор (выше плоскости разреза)
- портьеры (штора-волна)
- тюль (на плане — волнистая линия)
- римская или рулонная штора в проёме
- картина на стене — ширина в масштабе
- зеркало на стене — ширина в масштабе
- растение в кашпо — диаметр в масштабе
- ваза, настольный декор
- подушки, пледы — марки на мебели
- привязка от чистовой стены, мм
- (1) номер помещения, площадь м²
- стены (подложка обмера)
- * «*» — принято, не замерено и не подтверждено
- ** «**» — предложение проектировщика, заказчиком не утверждено

Т1, ДК1 — марки по ведомостям текстиля и декора

Экспликация помещений

лист 20 · на плане — номера в марках

Окна: шина → полотно, мм

Поз.	Шина	Верх шины	Полотно, низ
Т1, Т2	2150	2700, ниша	2690, низ 10
Т8, Т9	2140	2700, ниша	2690, низ 10
Т14	890	2700, ниша	1900, низ 800
Т16**, Т17**	1800	2700, ниша	1930, низ 770
Т22	2140	2600, ниша	1700, низ 900

Допущения и предложения на листе

Основа листа: размеры сняты с размерных цепочек растрового скана плана заказчика, на объекте не замерены; ступени наружного контура приведены к граням помещений модели (ИЗ-8, К-20, К-21); высота потолка 2700 мм принята, источника нет (К-24); тип дома и перекрытие (монолит, плита 220 мм) приняты, источника нет (К-3); толщины стен приняты (250 и 120 мм), источника нет (К-21); мощность 15 кВт принята, технических условий нет (К-25).

Знак «*» — принято, не замерено и не подтверждено (замерить на объекте): К-1, К-15: Ст К1-2, Ст В1-2; К-22: окно пом. 11 (стена В).

Знак «**» — предложение проектировщика, заказчиком не утверждено (согласовать с заказчиком): ИЗ-1: Т16, Т17; ДК16 — место перенесено (9900; 6100) → (10200; 4300), основание в данных не записано; ИЗ-1, К-1: окно пом. 9 (стена В); ИЗ-6: дверь пом. 12 (стена Г); ИЗ-7: ДК20, ДК21; ИЗ-8: дверь пом. 2 (стена В) — смещение 100 → 110 мм (откос до угла был 40 мм при норме от 50 мм).

См. лист открытых вопросов (лист 6, записи К-1, К-3; лист 7, записи К-15, К-20–К-22, К-24, К-25; лист 9, записи ИЗ-1, ИЗ-6, ИЗ-7; лист 10, запись ИЗ-8).

Примечания

1. Размеры — в мм. Отступы ковров — от чистовых стен; высоты картин и зеркал — от чистого пола до центра или низа рамы.
2. Шторы — на шинах в нишах потолка (ниша — план потолков, лист 44); закладная под шину — до обшивки ГКЛ. Схемы окон, длины полотен и сборка — лист 64.
3. Картины и зеркала массой более 5 кг — на анкеры по основанию, нагрузка крепежа не меньше двойной массы изделия; на ГКЛ — только по закладной. Декор не перекрывает розетки и выключатели.
4. Ковры на гладком полу — на противоскользящей подложке.
5. Мебель — по плану расстановки мебели (лист 24); ведомость текстиля — лист 65, ведомость декора и схемы развески — лист 66.
6. Знак «*» у проёма — допущение: положение и размеры проёма не замерены (окно пом. 11, стена В); размер напечатан как принятый. Реестр: листы 6–11, вопрос К-22.
7. Номера помещений — по экспликации (лист 20); наименования и площади на этом листе не дублируются.
8. Марки текстиля «Т» и декора «Д» относятся только к листам текстиля и декора; индексы трубопроводов Т1–Т4 — на листах ВК и ОВ.

1000 мм · печать 1:1

Изм.	Кол.уч	Лист	№ док.	Подп.	Дата
Разраб.		Кырлан А.С.			21.10.26
Пров.					
ГИП		Кырлан А.С.			21.10.26
Н. контр.					
Утв.					

ГД-2026-004-АИ

Четырёхкомнатная квартира

Общая площадь 102,67* м² · * размеры со скана, не замерены (реестр — л. 6–11, ИЗ-8, К-20, К-21)

Дизайн-проект интерьера четырёхкомнатной квартиры

Стадия	Лист	Листов
РП	63	124

План текстиля и декора

М 1:100

Кырлан Александр Сергеевич

выпуск 05.10.2026 № 7e7a2cd217 · стр. 72 из 168

08

Декор и текстиль

Кырлан Александр Сергеевич

выпуск 05.10.2026 · № 7e7a2cd217 · стр. 73 из 168

Шторы и карнизы

Схемы окон «шина → полотно» (М 1:100) · отметки от чистого пола помещения · размеры в мм

Окно 1 — Зал (пом. 1): Т1, Т2 (М 1:100)

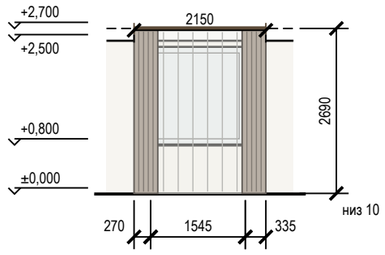

Окно 1 — Детская 1 (пом. 4): Т8, Т9 (М 1:100)

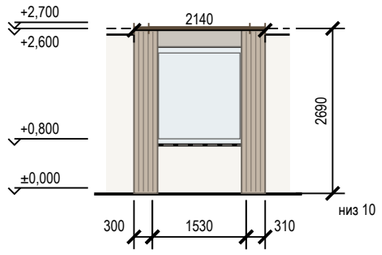

Окно 1 — Кухня (пом. 6): Т14 (М 1:100)

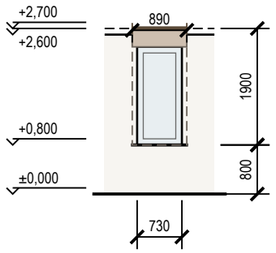

Окно 1 — Детская 2 (пом. 9): Т16**, Т17** (М 1:100)**

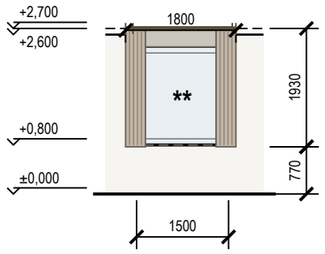

Окно 1 — Балкон 1 (пом. 13): Т22 (М 1:100)

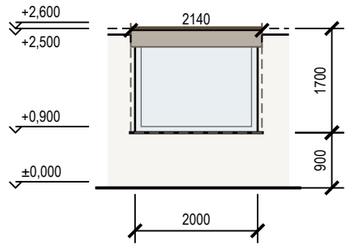

Карта окон: окно → шина → полотно

Поз.	Окно, пом.	Проём Ш×В, подоконник	Верх ниши	Изделие	Шина / карниз: длина, крепление	Верх шины	Полотно: длина, низ	Управление
Т1	1, пом. 1	1545×1600, подок. 800	+2,700	портьеры	шина, 2150, в нише потолка, вынос 150	+2,700	2690, низ 10 (парит)	вручную
Т2	1, пом. 1	1545×1600, подок. 800	+2,700	тюль	шина, 2150, в нише потолка, вынос 100	+2,700	2690, низ 10 (парит)	вручную
Т8	1, пом. 4	1530×1600, подок. 800	+2,700	портьеры	шина, 2140, в нише потолка, вынос 150	+2,700	2690, низ 10 (парит)	вручную
Т9	1, пом. 4	1530×1600, подок. 800	+2,700	римская штора	шина, 1650, в нише потолка, вынос 120	+2,700	1900, низ 800	без шнура
Т14	1, пом. 6	730×1600, подок. 800	+2,700	рулонная штора	шина, 890, в нише потолка, вынос 120	+2,700	1900, низ 800	без шнура
Т16**	1**, пом. 9	1500×1600, подок. 800	+2,700	портьеры	шина, 1800, в нише потолка, вынос 150	+2,700	1930, низ 770 (до подоконника)	вручную
Т17**	1**, пом. 9	1500×1600, подок. 800	+2,700	римская штора	шина, 1620, в нише потолка, вынос 120	+2,700	1900, низ 800	без шнура
Т22	1, пом. 13	2000×1700, подок. 900	+2,600	рулонная штора	шина, 2140, в нише потолка, вынос 120	+2,600	1700, низ 900	без шнура

Задания смежникам

Кому	Задание	Пом.
Гипсокартонщик	окно 1 (1545×1600, Т1, Т2): ниша под шторы 150×100, верх +2,700; закладная под шину L 2150 по всей длине — до обшивки	1
Гипсокартонщик	окно 1 (1530×1600, Т8, Т9): ниша под шторы 150×100, верх +2,700; закладная под шину L 2140 по всей длине — до обшивки	4
Гипсокартонщик	окно 1 (730×1600, Т14): ниша под шторы 150×100, верх +2,700; закладная под шину L 890 по всей длине — до обшивки	6
Гипсокартонщик	окно 1 (1500×1600, Т16**, Т17**): ниша под шторы 150×100, верх +2,700; закладная под шину L 1800 по всей длине — до обшивки	9
Гипсокартонщик	окно 1 (2000×1700, Т22): ниша под шторы 150×100, верх +2,600; закладная под шину L 2140 по всей длине — до обшивки	13
Электрик	выводы под электрокарнизы не требуются (управление вручную)	

Условные обозначения

- портьеры в открытом положении
- римская штора: сложена / опущена
- верх ниши под шторы в потолке
- ** — «**» — предложение проектировщика, заказчиком не утверждено
- тюль (на виде окна — прозрачная плашка)
- шина или карниз на отметке верха
- оконный проём

Допущения и предложения на листе

Основа листа: размеры сняты с размерных цепочек растрового скана плана заказчика, на объекте не замерены; ступени наружного контура приведены к граням помещений модели (ИЗ-8, К-20, К-21); высота потолка 2700 мм принята, источника нет (К-24); тип дома и перекрытие (монолит, плита 220 мм) приняты, источника нет (К-3); толщины стен приняты (250 и 120 мм), источника нет (К-21); мощность 15 кВт принята, технических условий нет (К-25).

Знак «**» — предложение проектировщика, заказчиком не утверждено (согласовать с заказчиком): ИЗ-1: Т16, Т17; ИЗ-1, К-1: окно пом. 9 (стена В).

См. лист открытых вопросов (лист 6, записи К-1, К-3; лист 7, записи К-20, К-21, К-24, К-25; лист 9, запись ИЗ-1; лист 10, запись ИЗ-8).

Примечания

1. Отметки — от чистого пола помещения; размеры — мм. Длины полотен уточняются замером после чистовой отделки пола и потолка, до раскроя.
2. Шины в нишах потолка: закладная (брус или профиль) по всей длине ниши — до обшивки ГКЛ; ниша и её отметка — узел ниши на плане потолков (лист 44).
3. Шина в нише — на отметке верха ниши (крепление к закладной в потолке ниши); длина полотна — от верха шины до чистого пола за вычетом зазора.
4. Полотно портьер «парит» над полом на 10 мм; сборка портьер — 2,0, тюля — 2,5 (ширина полотна — в ведомости текстиля).
5. Шнур римской шторы — с натяжителем, петля низом не ниже 1500 мм от пола (защита детей; EN 13120 — рекомендация).
6. Электрокарнизы не предусмотрены; при замене на электропривод — вывод кабеля в нише у края шины (задание электрику).
7. Длины шин и полотен окон 1 (пом. 9) выведены из размеров и положения проёма, а они — допущение: до раскроя полотен проём замерить, длины сверить.
8. Марки изделий — по плану текстиля и декора (лист 63) и ведомости текстиля (лист 65).

Изм.	Кол.уч	Лист	№ док.	Подп.	Дата
Разраб.		Кырлан А.С.			21.10.26
Пров.					
ГИП		Кырлан А.С.			21.10.26
Н. контр.					
Утв.					

ГД-2026-004-АИ

Четырёхкомнатная квартира

Общая площадь 102,67* м² · * размеры со скана, не замерены (реестр — л. 6–11, ИЗ-8, К-20, К-21)

Дизайн-проект интерьера четырёхкомнатной квартиры

Стадия	Лист	Листов
РП	64	124

Шторы и карнизы

М б/м

Кырлан Александр Сергеевич

выпуск 05.10.2026 № 7e7a2cd217 · стр. 74 из 168

Ведомость текстиля

Шторы, тюль, римские шторы, ковры, подушки и пледы · размеры в мм · марки — по плану текстиля и декора

Текстиль: шторы, ковры, подушки, пледы

Поз.	Пом.	Изделие	Размер, мм	Ткань, состав, плотность	Сборка, ширина полотна		Цвет (система, код)	Кол.	Примечание
T1	1	Портьеры-волна, два полотна	шина 2150 × полотно 2690	лён 100 %; 280 г/м²	× 2, ширина 4300		Tikkurila V486 (Claystone)	2	низ 10 (парит); в нише потолка; уход: химчистка; отпаривание на карнизе
T2	1	Тюль-вуаль, одно полотно	шина 2150 × полотно 2690	вуаль; полиэстер 100 %; 60 г/м²	× 2,5, ширина 5375		Tikkurila F497 (Paper)	1	низ 10 (парит); в нише потолка; уход: стирка 30 °C, вешать влажной
T3	1	Ковёр мягкой группы	2200×1050	шерсть, плоское плетение; шерсть 100 %			NCS S 3005-Y20R (тёплый тауп-серый)	1	противоскользящая подложка; ворс 8 мм; уход: сухая чистка, пылесос без турбощётки
T4	1	Подушки декоративные на диван	500×500	лён 100 %			Tikkurila H487 (Pumice)	3	на M2; уход: съёмный чехол, стирка 30 °C
T5	1	Подушки декоративные на диван, акцент	400×600	хлопковый бархат 100 %			Tikkurila L481 (Silhouette)	2	на M2; уход: химчистка
T6	1	Плед на диван	1300×1700	шерсть мериноса 100 %			Tikkurila L481 (Silhouette)	1	на M2; уход: ручная стирка 30 °C
T7	1	Раннер на обеденный стол	500×1800	лён 100 %			Tikkurila J484 (Castle)	1	на M7; уход: стирка 40 °C, глажение влажным
T8	4	Портьеры стационарные, два полотна	шина 2140 × полотно 2690	лён-хлопок; лён 55 %, хлопок 45 %; 260 г/м²	× 2, ширина 4280		Tikkurila V484 (Driftwood)	2	низ 10 (парит); в нише потолка; уход: химчистка
T9	4	Римская штора блэкаут	шина 1650 × полотно 1900	хлопок с блэкаут-подкладкой; хлопок 100 %, подкладка полиэстер; 300 г/м²			Tikkurila H487 (Pumice)	1	низ 800; в нише потолка; шнур: петля —, cordless; уход: сухая чистка
T10	4	Ковёр у кровати	2600×1900	шерсть, ручное ткачество; шерсть 80 %, хлопок 20 %			Tikkurila H487 (Pumice)	1	противоскользящая подложка; ворс 10 мм; уход: сухая чистка
T11	4	Подушки декоративные на кровать	500×500	лён 100 %			Tikkurila H487 (Pumice)	2	на M11; уход: съёмный чехол, стирка 30 °C
T12	4	Подушка декоративная, акцент	400×600	хлопковый бархат 100 %			NCS S 5010-B10G (серо-петроль)	1	на M11; уход: химчистка
T13	4	Плед на кровать	1400×2000	хлопок 100 %			NCS S 5010-B10G (серо-петроль)	1	на M11; уход: стирка 40 °C
T14	6	Рулонная штора кассетная, ткань димаут	шина 890 × полотно 1900	ткань димаут с грязеотталкивающей пропиткой; полиэстер 100 %			Tikkurila J484 (Castle)	1	низ 800; в нише потолка; шнур: петля —, cordless; уход: протирка влажной губкой
T15	7	Ковёр прихожей, низкий ворс	1500×1100	шерсть, петлевое плетение; шерсть 80 %, полиамид 20 %			NCS S 3005-Y20R (тёплый тауп-серый)	1	противоскользящая подложка; ворс 6 мм; уход: сухая чистка
T16**	9	Портьеры стационарные, два полотна, до подоконника	шина 1800 × полотно 1930	лён-хлопок; лён 55 %, хлопок 45 %; 260 г/м²	× 2, ширина 3600		Tikkurila V484 (Driftwood)	2	низ 770 (до подоконника); в нише потолка; уход: химчистка
T17**	9	Римская штора блэкаут	шина 1620 × полотно 1900	хлопок с блэкаут-подкладкой; хлопок 100 %, подкладка полиэстер; 300 г/м²			Tikkurila H487 (Pumice)	1	низ 800; в нише потолка; шнур: петля —, cordless; уход: сухая чистка
T18	9	Ковёр игровой зоны	1700×1400	шерсть, ручное ткачество; шерсть 100 %			NCS S 3005-Y20R (тёплый тауп-серый)	1	противоскользящая подложка; ворс 12 мм; уход: сухая чистка
T19	9	Подушки декоративные на кровать	450×450	лён 100 %			Tikkurila H487 (Pumice)	2	на M34; уход: съёмный чехол, стирка 30 °C
T20	9	Подушка декоративная, акцент	400×600	букле; шерсть 60 %, полиэстер 40 %			Farrow & Ball No. 47 (Green Smoke)	1	на M34; уход: химчистка
T21	9	Плед на кровать	1300×1900	хлопок 100 %			Farrow & Ball No. 47 (Green Smoke)	1	на M34; уход: стирка 40 °C
T22	13	Рулонная штора кассетная, солнцезащитная	шина 2140 × полотно 1700	ткань димаут, солнцезащитная; полиэстер 100 %			Tikkurila V486 (Claystone)	1	низ 900; в нише потолка; шнур: петля —, cordless; уход: протирка влажной губкой
T23	13	Плед на кресло M43	1300×1700	шерсть 100 %			Tikkurila V484 (Driftwood)	1	на M43; уход: ручная стирка 30 °C

образец цвета — по HEX производителя краски, справочно

Итого: шторы и тюль — 11 шт.; ковры и дорожки — 4 шт.; подушки, пледы, покрывала — 16 шт.

Примечания

1. Коды цвета — ориентир подбора по веерам производителей красок; ткань утверждается по образцу при дневном свете и при свете проекта 2700–3000 K.
2. Размеры полотен — по замеру после чистовой отделки пола и потолка; ширина полотна указана с учётом сборки, без припусков на швы. Схемы окон и отметки шин лист 64.
3. Портьеры и тюль — на тесьме «волна» по системе шины; блэкаут — подкладкой. Ковры — на противоскользящей подложке.
4. Замена изделия — аналогом по характеристикам (состав, плотность, размер, цвет по образцу) с согласованием автора проекта.
5. Места изделий — план текстиля и декора (лист 63); подушки и пледы — по марке мебели.

Допущения и предложения на листе

Основа листа: размеры сняты с размерных цепочек растрового скана плана заказчика, на объекте не замерены; ступени наружного контура приведены к граням помещений модели (ИЗ-8, К-20, К-21); высота потолка 2700 мм принята, источника нет (К-24); тип дома и перекрытие (монолит, плита 220 мм) приняты, источника нет (К-3); толщины стен приняты (250 и 120 мм), источника нет (К-21); мощность 15 кВт принята, технических условий нет (К-25).

Знак «**» — предложение проектировщика, заказчиком не утверждено (согласовать с заказчиком): ИЗ-1: T16, T17.

См. лист открытых вопросов (лист 6, запись К-3; лист 7, записи К-20, К-21, К-24, К-25; лист 9, запись ИЗ-1; лист 10, запись ИЗ-8).

Изм.	Кол.уч	Лист	№ док.	Подп.	Дата
Разраб.		Кырлан А.С.			21.10.26
Пров.					
ГИП		Кырлан А.С.			21.10.26
Н. контр.					
Утв.					

ГД-2026-004-АИ

Четырёхкомнатная квартира

Общая площадь 102,67* м² · * размеры со скана, не замерены (реестр — л. 6–11, ИЗ-8, К-20, К-21)

Дизайн-проект интерьера четырёхкомнатной квартиры

Стадия	Лист	Листов
РП	65	124

Ведомость текстиля

М б/м

Кырлан Александр Сергеевич

выпуск 05.10.2026 № 7e7a2cd217 · стр. 75 из 168

Ведомость декора. Схемы развески

ПРЕДВАРИТЕЛЬНО · не для производства работ · открыто пунктов: 30 (реестр — л. 6–11)

Картины, зеркала, растения, настольный декор · схемы развески (М 1:100) · высоты — мм от чистого пола

Декор: картины, зеркала, растения, предметы

картина · зеркало · мебель под изделием

Поз.	Пом.	Предмет	Размер, мм	Место: стена, высота от пола, мм	Масса, кг	Крепёж и основание	Свет места, отделка	Кол.
ДК1	1	Картина над диваном: Песочные и грейжевые поля, холст	1400×900	стена В, привязка 1150; низ 1000, центр 1450; над М2	6	планка на дюбелях, 4 точки; основание: перегородка 120 мм; нагрузка 20 кг		1
ДК2	1	Зеркало над буфетом, рама шпон дуба	1000×800	стена А, привязка 3650; низ 1100, центр 1500; над М6	12	анкер химический, 4 точки; основание: монолит, наружная стена; нагрузка 30 кг		1
ДК3	1	Фикус лировидный в кашпо Ø400	450×450	напольное			свет яркий рассеянный	1
ДК4	2	Зеркало над раковиной П3, влагостойкое	600×800	стена В, привязка 825; низ 1100, центр 1500	5	зеркалодержатели, 4 точки; основание: перегородка 120 мм, керамогранит; нагрузка 20 кг		1
ДК5	4	Картина над изголовьем: Звёздная карта, тушь	1100×700	стена А, привязка 1300; низ 1300, центр 1650; над М11	4	две петли на дюбелях; основание: монолит, наружная стена; нагрузка 15 кг		1
ДК6	4	Зеркало над комодом М17	700×900	стена В, привязка 2910; низ 1050, центр 1500; над М17	8	анкер химический, 4 точки; основание: перегородка 120 мм; нагрузка 24 кг		1
ДК7	4	Хлорофитум хохлатый в напольном кашпо Ø380	420×420	напольное			свет средний	1
ДК8	6	Часы настенные Ø400	400×400	стена В, привязка 1200; центр 1550	2	дюбель с крюком, 1 точка; основание: перегородка 120 мм; нагрузка 10 кг		1
ДК9	6	Хлорофитум хохлатый на подоконнике (отм. +0,800)	300×200	напольное			свет средний	1
ДК10	7	Зеркало над консолью М31	700×1000	стена А, привязка 490; низ 1050, центр 1550; над М31	9	анкер химический, 4 точки; основание: перегородка 120 мм; нагрузка 25 кг		1
ДК11	7	Замиокулькас в напольном кашпо Ø360	400×400	напольное			свет слабый	1
ДК12	9	Картина над изголовьем: Ветка клёна, гравюра	600×800	стена А, привязка 150; низ 1200, центр 1600; над М34	3	две петли на дюбелях; основание: перегородка 120 мм; нагрузка 12 кг		1
ДК13	9	Постер в раме, левый (группа «постеры»): Лиса в лесу	400×500	стена Г, привязка 280; низ 1250, центр 1500	2	петля на дюбеле; основание: перегородка 120 мм; нагрузка 10 кг		1
ДК14	9	Постер в раме, средний (группа «постеры»): Медведь у озера	400×500	стена Г, привязка 750; низ 1250, центр 1500	2	петля на дюбеле; основание: перегородка 120 мм; нагрузка 10 кг		1
ДК15	9	Постер в раме, правый (группа «постеры»): Сова под луной	400×500	стена Г, привязка 1220; низ 1250, центр 1500	2	петля на дюбеле; основание: перегородка 120 мм; нагрузка 10 кг		1
ДК16**	9	Спатифиллум в напольном кашпо Ø360	400×400	напольное			свет средний	1
ДК17	10	Зеркало над раковиной П9, влагостойкое	500×700	стена Б, привязка 290; низ 1150, центр 1500	4	зеркалодержатели, 4 точки; основание: перегородка 120 мм, керамогранит; нагрузка 16 кг		1
ДК18	12	Зеркало ростовое 500×1600	500×1600	стена В, привязка 640; низ 250, центр 1050	12	анкер химический, 4 точки + опора снизу; основание: перегородка 120 мм; нагрузка 30 кг		1
ДК19	13	Лавр благородный в напольном кашпо Ø380	400×400	напольное			свет яркий рассеянный	1
ДК20**	11	Картина: Глубокий лиловый с песочным просветом, холст	800×600	стена Г, привязка 640; низ 1300, центр 1600	4	планка на дюбелях, 2 точки; основание: перегородка 120 мм; нагрузка 8 кг	Tikkurila L481 (Silhouette)	1
ДК21**	11	Ваза напольная, керамика матовая	300×300	напольное			Tikkurila L481 (Silhouette)	1

ДК1 — Зал (пом. 1), стена В (М 1:100)

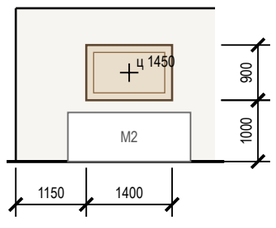

ДК2 — Зал (пом. 1), стена А (М 1:100)

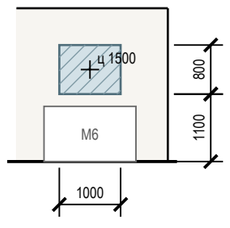

ДК4 — Ванная комната (пом. 2), стена В (М 1:100)

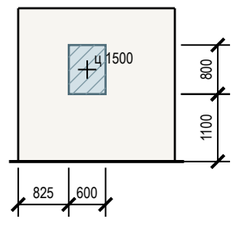

ДК5 — Детская 1 (пом. 4), стена А (М 1:100)

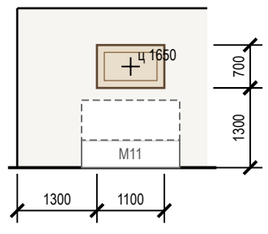

ДК6 — Детская 1 (пом. 4), стена В (М 1:100)

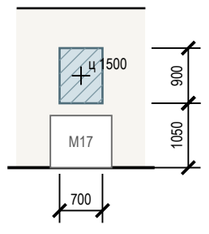

ДК8 — Кухня (пом. 6), стена В (М 1:100)

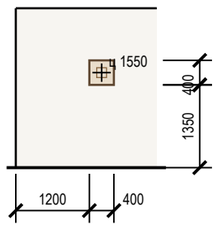

ДК10 — Прихожая-коридор (пом. 7), стена А (М 1:100)

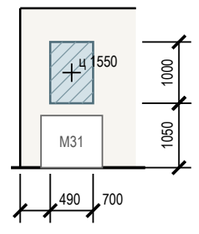

Допущения и предложения на листе

Основа листа: размеры сняты с размерных цепочек растрового скана плана заказчика, на объекте не замерены; ступени наружного контура приведены к граням помещений модели (ИЗ-8, К-20, К-21); высота потолка 2700 мм принята, источника нет (К-24); тип дома и перекрытие (монолит, плита 220 мм) приняты, источника нет (К-3); толщины стен приняты (250 и 120 мм), источника нет (К-21); мощность 15 кВт принята, технических условий нет (К-25).

Знак «**» — предложение проектировщика, заказчиком не утверждено (согласовать с заказчиком): ИЗ-1: ДК16 — место перенесено (9900; 6100) → (10200; 4300), основание в данных не записано; ИЗ-7: ДК20, ДК21.

См. лист открытых вопросов (лист 6, запись К-3; лист 7, записи К-20, К-21, К-24, К-25; лист 9, записи ИЗ-1, ИЗ-7; лист 10, запись ИЗ-8).

Примечания

1. Высоты — от чистого пола помещения до низа изделия, «ц» — до центра; привязки — от чистовой грани угла стены, мм.
2. Над мебелью низ изделия — на 150–250 мм выше спинки или изголовья; без мебели центр — на 1450–1600 мм от пола.
3. Изделия до 5 кг — на два подвеса по основанию; тяжелее — на анкеры с нагрузкой не меньше двойной массы; на ГКЛ — только по закладной или анкеру для пустотелых оснований.
4. Зеркала в рост — с креплением от опрокидывания; в санузлах — влагостойкие, на клей для зеркал и нейтральный силикон.
5. Места изделий — план текстиля и декора (лист 63). Схемы ДК12, ДК13, ДК14, ДК15, ДК17, ДК18, ДК20** — по ведомости и плану.

Изм.	Кол.уч	Лист	№ док.	Подп.	Дата
Разраб.		Кырлан А.С.			21.10.26
Пров.					
ГИП		Кырлан А.С.			21.10.26
Н. контр.					
Утв.					

ГД-2026-004-АИ

Четырёхкомнатная квартира

Общая площадь 102,67* м² · * размеры со скана, не замерены (реестр — л. 6–11, ИЗ-8, К-20, К-21)

Дизайн-проект интерьера четырёхкомнатной квартиры

Стадия	Лист	Листов
РП	66	124

Ведомость декора. Схемы развески

М б/м

Кырлан Александр Сергеевич

выпуск 05.10.2026 № 7e7a2cd217 · стр. 76 из 168

Встроенная мебель. Схема расположения

встроенная и корпусная мебель на заказ, кухонный гарнитур · размеры в мм · марки — по ведомости изделий

ПРЕДВАРИТЕЛЬНО · не для производства работ · открыто пунктов: 30 (реестр — л. 6–11)

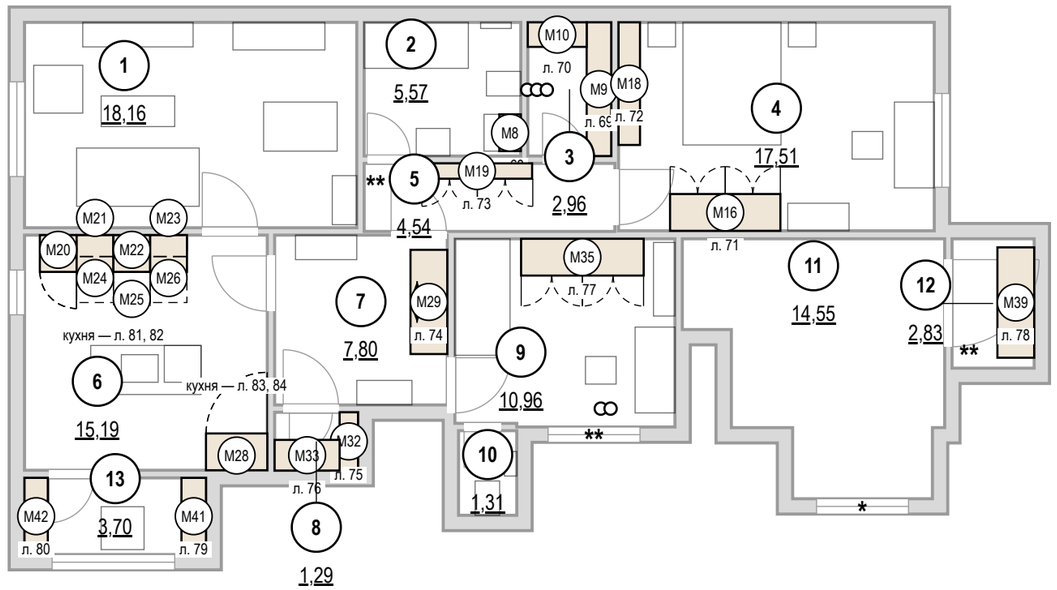

Ведомость изделий

Марка	Наименование	Пом.	Ш×Г×В, мм	Лист
M8	Система хранения	2	600×350×700	68
M9	Система хранения	3	2180×400×2400	69
M10	Система хранения	3	960×400×2400	70
M16	Шкаф распашной	4	1800×600×2400	71
M18	Система хранения	4	2000×350×2100	72
M19	Система хранения	5	1800×250×2400	73
M29	Шкаф-купе	7	1700×600×2400	74
M32	Система хранения	8	950×300×2400	75
M33	Система хранения	8	1060×500×300	76
M35	Шкаф распашной	9	2000×600×2400	77
M39	Система хранения	12	1800×600×2400	78
M41	Система хранения	13	1250×400×2000	79
M42	Система хранения	13	1250×380×2000	80
M20	Пенал: холодильник встр.	6	600×600×2300	81
M21	Модуль нижний: ящики	6	600×600×900	81
M24	Модуль навесной: полки	6	600×350×720	81
M22	Модуль нижний: духовой шкаф, варочная	6	600×600×900	81
M25	Модуль навесной: полки	6	600×350×600	81
M23	Модуль нижний: ящики	6	600×600×900	81
M26	Модуль навесной: полки	6	600×350×720	81
M28	Пенал: полки	6	1000×600×2300	83

Условные обозначения

- изделие мебельщика: корпус на полу
- навесной модуль (невидимый контур)
- открывание распашного фасада
- зона выдвижения ящика, двери техники
- дверь купе, стрелка — направление движения
- П5 — марка изделия, под ней — лист изделия
- * — «*» — принято, не замерено и не подтверждено
- ** — «**» — предложение проектировщика, заказчиком не утверждено

Допущения и предложения на листе

Основа листа: размеры сняты с размерных цепочек растрового скана плана заказчика, на объекте не замерены; ступени наружного контура приведены к граням помещений модели (ИЗ-8, К-20, К-21); высота потолка 2700 мм принята, источника нет (К-24); тип дома и перекрытие (монолит, плита 220 мм) приняты, источника нет (К-3); толщины стен приняты (250 и 120 мм), источник нет (К-21); мощность 15 кВт принята, технических условий нет (К-25).

Знак «*» — принято, не замерено и не подтверждено (замерить на объекте): К-1, К-15: Ст К1-2, Ст В1-2; К-22: окно пом. 11 (стена В).

Знак «**» — предложение проектировщика, заказчиком не утверждено (согласовать с заказчиком): ИЗ-1, К-1: окно пом. 9 (стена В); ИЗ-6: дверь пом. 12 (стена Г); ИЗ-8: дверь пом. 2 (стена В) — смещение 100 → 110 мм (откос до угла был 40 мм при норме от 50 мм).

См. лист открытых вопросов (лист 6, записи К-1, К-3; лист 7, записи К-15, К-20–К-22, К-24, К-25; лист 9, записи ИЗ-1, ИЗ-6; лист 10, запись ИЗ-8).

Примечания

1. Изделия — по чистовым размерам помещений; перед раскроем — контрольный замер цеха после чистовой отделки стен, пола и потолка.
2. Открывание фасадов и выдвижение ящиков показано в открытом положении: зоны не пересекают двери, радиаторы, выключатели и проходы.
3. Стояки и счётчики за мебелью — с сервисным люком; газовые трубы мебелью не зашиваются.
4. Покупная мебель — по плану расстановки мебели и спецификации дизайнера; здесь — подложкой.
5. Знак «*» у проёма — положение и размеры не замерены; реестр: листы 6–11, вопрос К-22.

1000 мм · печать 1:1

Изм.	Кол.уч	Лист	№ док.	Подп.	Дата
Разраб.		Кырлан А.С.			21.10.26
Пров.					
ГИП		Кырлан А.С.			21.10.26
Н. контр.					
Утв.					

ГД-2026-004-АИ

Четырёхкомнатная квартира

Общая площадь 102,67* м² · * размеры со скана, не замерены (реестр — л. 6–11, ИЗ-8, К-20, К-21)

Дизайн-проект интерьера четырёхкомнатной квартиры

Стадия	Лист	Листов
РП	67	124

Встроенная мебель. Схема расположения

М 1:100

Кырлан Александр Сергеевич

выпуск 05.10.2026 № 7e7a2cd217 · стр. 77 из 168

Система хранения М8

Ванная комната (пом. 2) · вид из помещения · размеры в мм, отметки в м

ПРЕДВАРИТЕЛЬНО · не для производства работ · открыто пунктов: 30 (реестр — л. 6–11)

Общий вид

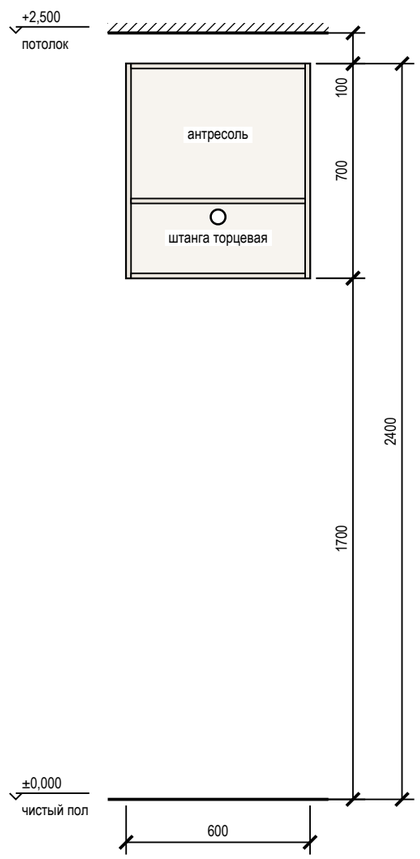

Наполнение, размеры в свету

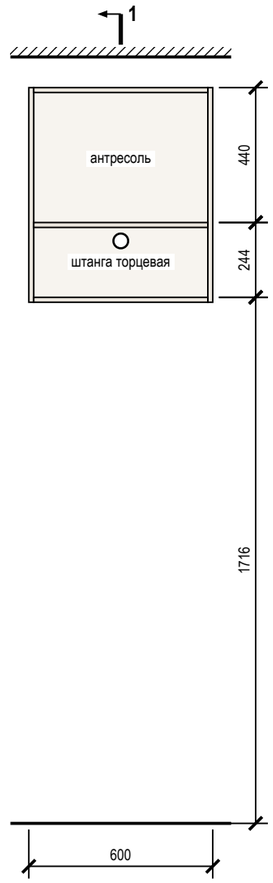

Разрез 1-1

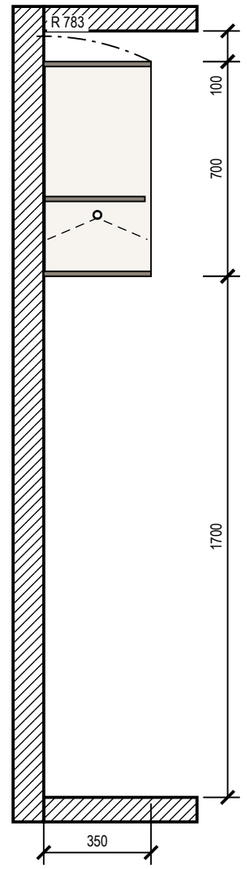

Примечания

1. Размеры — в мм по чистовой отделке; изделие 600×350×700 (Ш×Г×В). Перед раскроем — контрольный замер цеха после чистовой отделки стен, пола и потолка.
2. Корпус — ЛДСП 16 мм, задняя стенка ХДФ 4 мм в паз, цоколь 0 мм на регулируемых опорах; открытая система без фасадов, ящики с фасадами.
3. Кромка: скрытые торцы 0,4 мм, видимые 2 мм (ПВХ/АБС).
4. Номинальные зазоры: между фасадами ящиков 3 мм, фасад ящика — стойка 2 мм.
5. Ящики — направляющие полного выдвижения NL 300 (внутренняя глубина 346 мм ≥ NL + 3); присадка по 32-й системе — выполняет цех.
6. Зазор до потолка 100 мм — закрыть планкой в цвет корпуса при монтаже.
7. Подъём корпуса: диагональ боковины $\sqrt{(700^2 + 350^2)} = 783$ мм < 800 мм до потолка — корпус собирается лёжа и поднимается поворотом.
8. Крепление к стене от опрокидывания: крепление к стене, 2 точки; основание стены и шаг анкеров — монтажная схема шкафов.

Условные обозначения

- корпус и полки ЛДСП (вид на стену)
- задняя стенка ХДФ
- деталь в разрезе
- штанга для плечиков (на разрезе — плечики 450 мм)
- траектория угла корпуса при подъёме в проектное положение

Допущения и предложения на листе

Основа листа: размеры сняты с размерных цепочек растрового скана плана заказчика, на объекте не замерены; ступени наружного контура приведены к граням помещений модели (ИЗ-8, К-20, К-21); высота потолка 2700 мм принята, источника нет (К-24); тип дома и перекрытие (монолит, плита 220 мм) приняты, источника нет (К-3); толщины стен приняты (250 и 120 мм), источника нет (К-21); мощность 15 кВт принята, технических условий нет (К-25).
См. лист открытых вопросов (лист 6, запись К-3; лист 7, записи К-20, К-21, К-24, К-25; лист 10, запись ИЗ-8).

1000 мм · печать 1:1

Изм.	Кол.уч	Лист	№ док.	Подп.	Дата
Разраб.		Кырлан А.С.			21.10.26
Пров.					
ГИП		Кырлан А.С.			21.10.26
Н. контр.					
Утв.					

ГД-2026-004-АИ

Четырёхкомнатная квартира

Общая площадь 102,67* м² · * размеры со скана, не замерены (реестр — л. 6–11, ИЗ-8, К-20, К-21)

Дизайн-проект интерьера четырёхкомнатной квартиры

Стадия	Лист	Листов
РП	68	124

Система хранения М8

М 1:20

Кырлан Александр Сергеевич

выпуск 05.10.2026 № 7e7a2cd217 · стр. 78 из 168

Система хранения M9

Тёмная комната (пом. 3) · вид из помещения · размеры в мм, отметки в м

ПРЕДВАРИТЕЛЬНО · не для производства работ · открыто пунктов: 30 (реестр — л. 6–11)

Общий вид

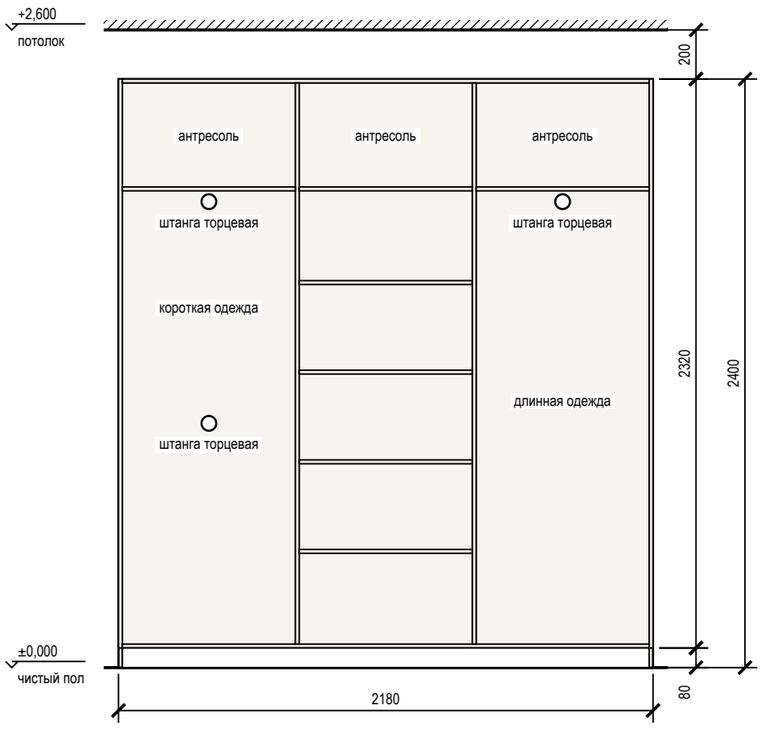

Наполнение, размеры в свету

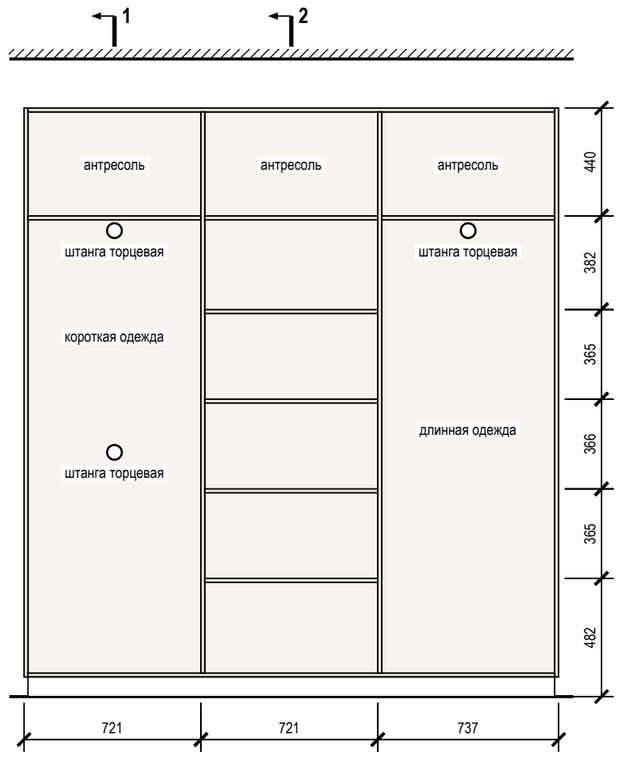

Разрез 1-1

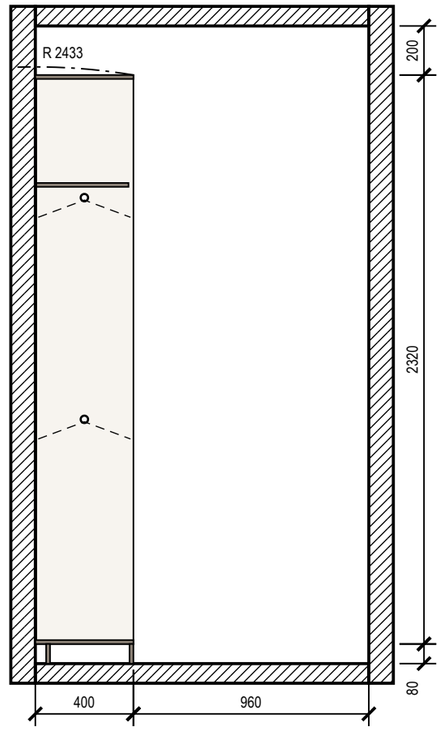

Разрез 2-2

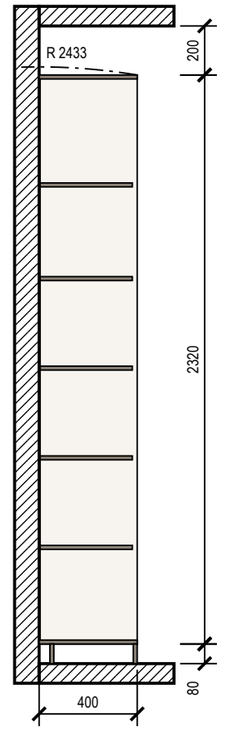

Примечания

1. Размеры — в мм по чистовой отделке; изделие 2180×400×2400 (Ш×Г×В). Перед раскроем — контрольный замер цеха после чистовой отделки стен, пола и потолка.
2. Корпус — ЛДСП 16 мм, задняя стенка ХДФ 4 мм в паз, цоколь 80 мм на регулируемых опорах; открытая система без фасадов, ящики с фасадами.
3. Кромка: скрытые торцы 0,4 мм, видимые 2 мм (ПВХ/АБС).
4. Номинальные зазоры: между фасадами ящиков 3 мм, фасад ящика — стойка 2 мм.
5. Ящики — направляющие полного выдвижения NL 350 (внутренняя глубина 396 мм ≥ NL + 3); присадка по 32-й системе — выполняет цех.
6. Зазор до потолка 200 мм.
7. Подъём корпуса: диагональ боковины $\sqrt{(2400^2 + 400^2)} = 2433$ мм < 2600 мм до потолка — корпус собирается лёжа и поднимается поворотом.
8. Крепление к стене от опрокидывания: крепление к стене, 4 точки; основание стены и шаг анкеров — монтажная схема шкафов.
9. Проход перед изделием 960 мм показан на разрезе 1-1.

Условные обозначения

- корпус и полки ЛДСП (вид на стену)
- задняя стенка ХДФ
- деталь в разрезе
- штанга для плечиков (на разрезе — плечики 450 мм)
- траектория угла корпуса при подъёме в проектное положение

Допущения и предложения на листе

Основа листа: размеры сняты с размерных цепочек растрового скана плана заказчика, на объекте не замерены; ступени наружного контура приведены к граням помещений модели (ИЗ-8, К-20, К-21); высота потолка 2700 мм принята, источника нет (К-24); тип дома и перекрытие (монолит, плита 220 мм) приняты, источника нет (К-3); толщины стен приняты (250 и 120 мм), источника нет (К-21); мощность 15 кВт принята, технических условий нет (К-25).

См. лист открытых вопросов (лист 6, запись К-3; лист 7, записи К-20, К-21, К-24, К-25; лист 10, запись ИЗ-8).

1000 мм · печать 1:1

Изм.	Кол.уч	Лист	№ док.	Подп.	Дата
Разраб.		Кырлан А.С.			21.10.26
Пров.					
ГИП		Кырлан А.С.			21.10.26
Н. контр.					
Утв.					

ГД-2026-004-АИ

Четырёхкомнатная квартира

Общая площадь 102,67* м² · * размеры со скана, не замерены (реестр — л. 6–11, ИЗ-8, К-20, К-21)

Дизайн-проект интерьера четырёхкомнатной квартиры

Стадия	Лист	Листов
РП	69	124

Система хранения M9

М 1:25

Кырлан Александр Сергеевич

выпуск 05.10.2026 № 7e7a2cd217 · стр. 79 из 168

Система хранения М10

Тёмная комната (пом. 3) · вид из помещения · размеры в мм, отметки в м

ПРЕДВАРИТЕЛЬНО · не для производства работ · открыто пунктов: 30 (реестр — л. 6–11)

Общий вид

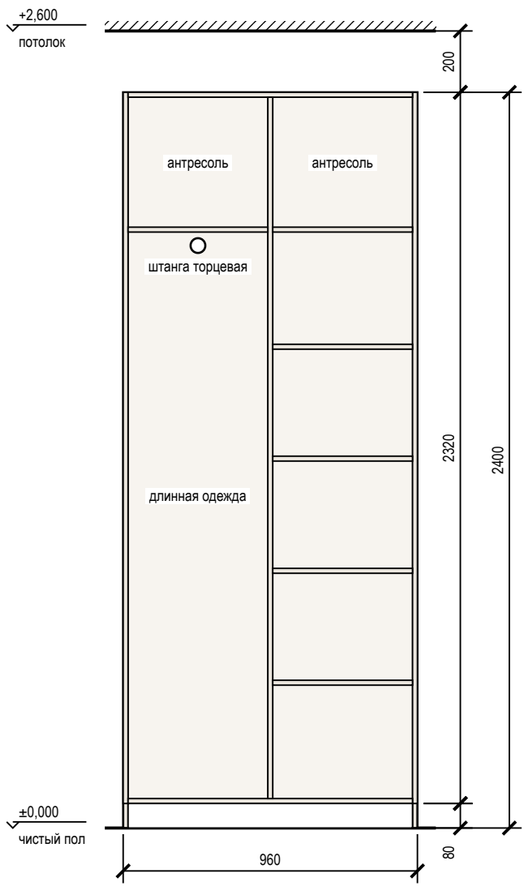

Наполнение, размеры в свету

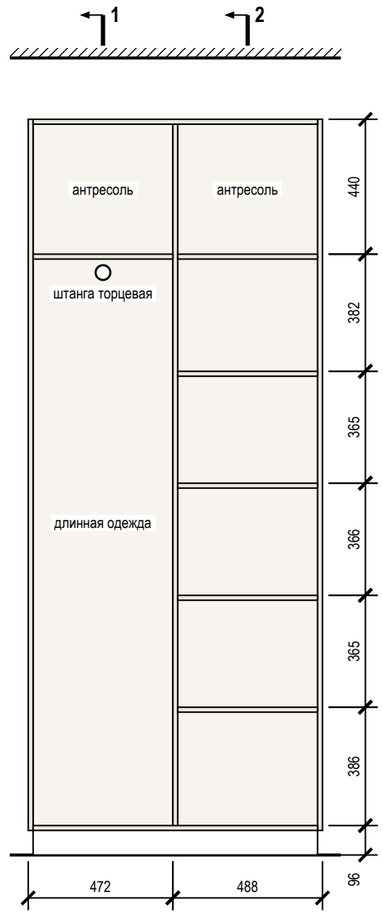

Разрез 1-1

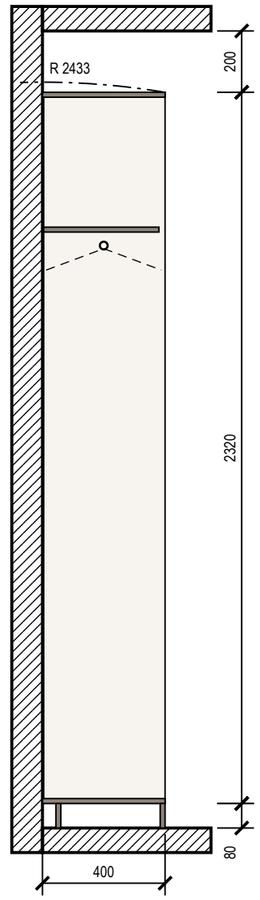

Разрез 2-2

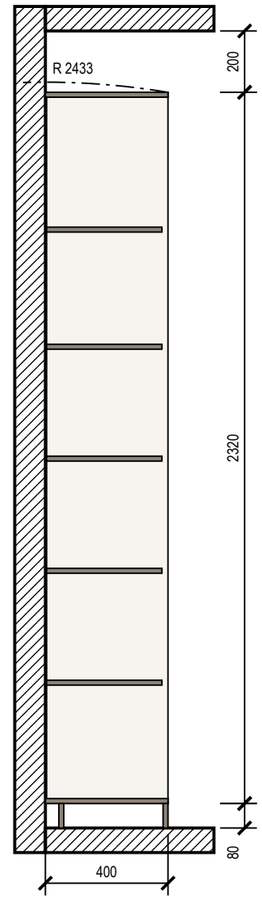

Примечания

1. Размеры — в мм по чистовой отделке; изделие 960×400×2400 (Ш×Г×В). Перед раскроем — контрольный замер цеха после чистовой отделки стен, пола и потолка.
2. Корпус — ЛДСП 16 мм, задняя стенка ХДФ 4 мм в паз, цоколь 80 мм на регулируемых опорах; открытая система без фасадов, ящики с фасадами.
3. Кромка: скрытые торцы 0,4 мм, видимые 2 мм (ПВХ/АБС).
4. Номинальные зазоры: между фасадами ящиков 3 мм, фасад ящика — стойка 2 мм.
5. Ящики — направляющие полного выдвижения NL 350 (внутренняя глубина 396 мм ≥ NL + 3); присадка по 32-й системе — выполняет цех.
6. Зазор до потолка 200 мм.
7. Подъём корпуса: диагональ боковины $\sqrt{(2400^2 + 400^2)} = 2433$ мм < 2600 мм до потолка — корпус собирается лёжа и поднимается поворотом.
8. Крепление к стене от опрокидывания: крепление к стене, 3 точки; основание стены и шаг анкеров — монтажная схема шкафов.

Условные обозначения

- корпус и полки ЛДСП (вид на стену)
- задняя стенка ХДФ
- деталь в разрезе
- штанга для плечиков (на разрезе — плечики 450 мм)
- траектория угла корпуса при подъёме в проектное положение

Допущения и предложения на листе

Основа листа: размеры сняты с размерных цепочек растрового скана плана заказчика, на объекте не замерены; ступени наружного контура приведены к граням помещений модели (ИЗ-8, К-20, К-21); высота потолка 2700 мм принята, источника нет (К-24); тип дома и перекрытие (монолит, плита 220 мм) приняты, источника нет (К-3); толщины стен приняты (250 и 120 мм), источника нет (К-21); мощность 15 кВт принята, технических условий нет (К-25).
См. лист открытых вопросов (лист 6, запись К-3; лист 7, записи К-20, К-21, К-24, К-25; лист 10, запись ИЗ-8).

1000 мм · печать 1:1

Изм.	Кол.уч	Лист	№ док.	Подп.	Дата
Разраб.		Кырлан А.С.			21.10.26
Пров.					
ГИП		Кырлан А.С.			21.10.26
Н. контр.					
Утв.					

ГД-2026-004-АИ

Четырёхкомнатная квартира

Общая площадь 102,67* м² · * размеры со скана, не замерены (реестр — л. 6–11, ИЗ-8, К-20, К-21)

Дизайн-проект интерьера четырёхкомнатной квартиры

Стадия	Лист	Листов
РП	70	124

Система хранения М10

М 1:20

Кырлан Александр Сергеевич

выпуск 05.10.2026 № 7e7a2cd217 · стр. 80 из 168

Шкаф распашной М16

Детская 1 (пом. 4) · вид из помещения · размеры в мм, отметки в м

ПРЕДВАРИТЕЛЬНО · не для производства работ · открыто пунктов: 30 (реестр — л. 6–11)

Вид с фасадами

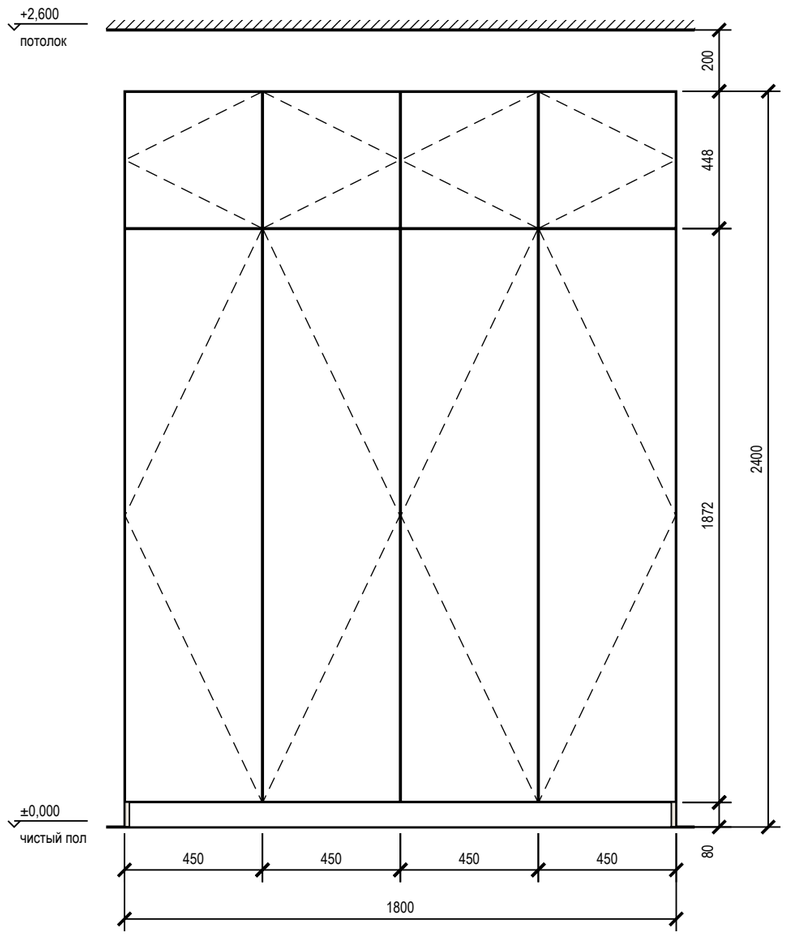

Вид без фасадов

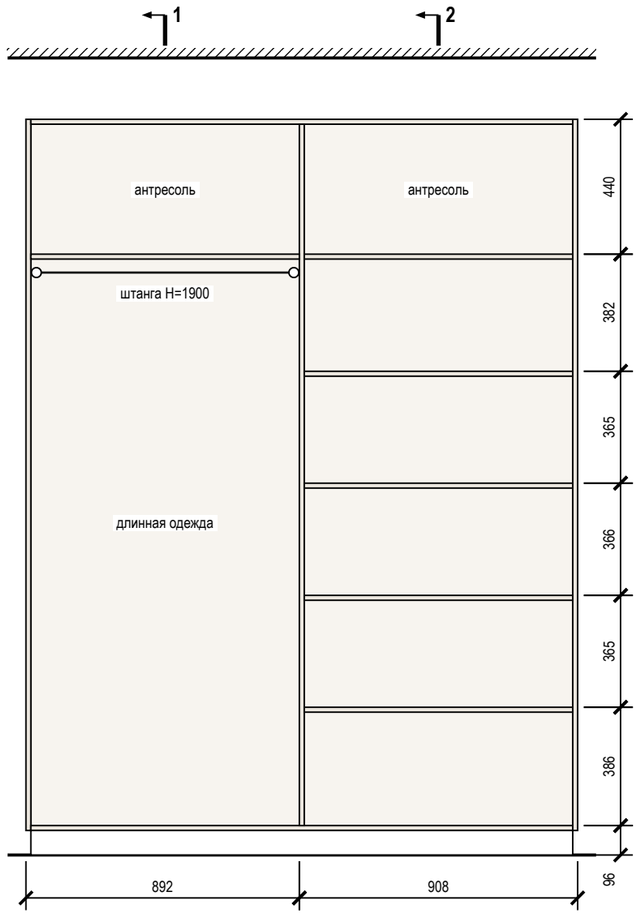

Разрез 1-1

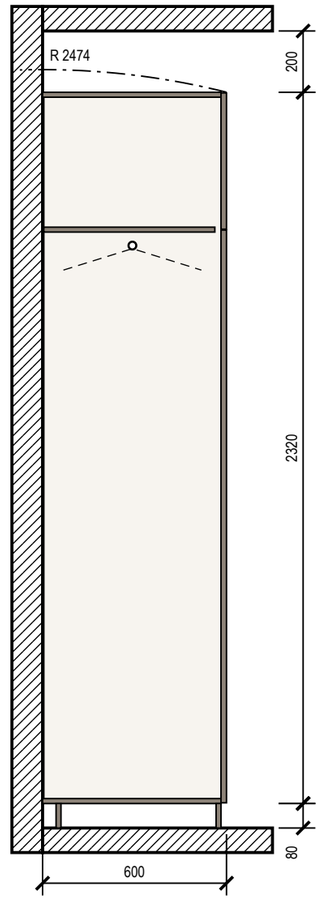

Разрез 2-2

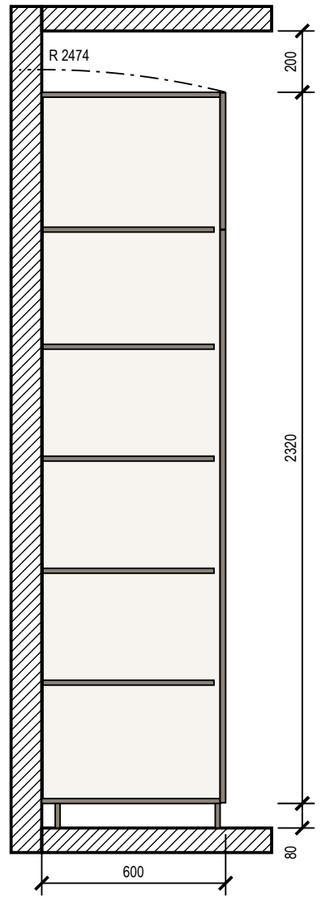

Примечания

1. Размеры — в мм по чистовой отделке; изделие 1800×600×2400 (Ш×Г×В). Перед раскроем — контрольный замер цеха после чистовой отделки стен, пола и потолка.
2. Корпус — ЛДСП 16 мм, задняя стенка ХДФ 4 мм в паз, цоколь 80 мм на регулируемых опорах; фасады — МДФ, эмаль матовая 18 мм накладные, цвет — по колерной карте; петли с доводчиком: фасад 1869 мм — 4 петли, фасад 445 мм — 2 петли.
3. Кромка: скрытые торцы 0,4 мм, видимые 2 мм (ПВХ/АБС).
4. Номинальные зазоры: между фасадами 3 мм, фасад — стена и фасад — потолок не менее 3 мм, фасад ящика — стойка 2 мм.
5. Ящики — направляющие полного выдвижения NL 550 (внутренняя глубина 578 мм ≥ NL + 3); присадка по 32-й системе — выполняет цех.
6. Зазор до потолка 200 мм.
7. Подъём корпуса: диагональ боковины $\sqrt{(2400^2 + 600^2)}$ = 2474 мм < 2600 мм до потолка — корпус собирается лёжа и поднимается поворотом.
8. Крепление к стене от опрокидывания: уголок к стене, 3 шт.; основание стены и шаг анкеров — монтажная схема шкафов.

Условные обозначения

- фасад распашной: линии сходятся к стороне петель
- корпус и полки ЛДСП (вид на стену)
- задняя стенка ХДФ
- деталь в разрезе
- штанга для плечиков (на разрезе — плечики 450 мм)
- траектория угла корпуса при подъёме в проектное положение

Допущения и предложения на листе

Основа листа: размеры сняты с размерных цепочек растрового скана плана заказчика, на объекте не замерены; ступени наружного контура приведены к граням помещений модели (ИЗ-8, К-20, К-21); высота потолка 2700 мм принята, источника нет (К-24); тип дома и перекрытие (монолит, плита 220 мм) приняты, источника нет (К-3); толщины стен приняты (250 и 120 мм), источника нет (К-21); мощность 15 кВт принята, технических условий нет (К-25).
См. лист открытых вопросов (лист 6, запись К-3; лист 7, записи К-20, К-21, К-24, К-25; лист 10, запись ИЗ-8).

1000 мм · печать 1:1

Изм.	Кол.уч	Лист	№ док.	Подп.	Дата
Разраб.		Кырлан А.С.			21.10.26
Пров.					
ГИП		Кырлан А.С.			21.10.26
Н. контр.					
Утв.					

ГД-2026-004-АИ

Четырёхкомнатная квартира

Общая площадь 102,67* м² · * размеры со скана, не замерены (реестр — л. 6–11, ИЗ-8, К-20, К-21)

Дизайн-проект интерьера четырёхкомнатной квартиры

Стадия	Лист	Листов
РП	71	124

Шкаф распашной М16

М 1:20

Кырлан Александр Сергеевич

выпуск 05.10.2026 № 7e7a2cd217 · стр. 81 из 168

Система хранения M18

Детская 1 (пом. 4) · вид из помещения · размеры в мм, отметки в м

ПРЕДВАРИТЕЛЬНО · не для производства работ · открыто пунктов: 30 (реестр — л. 6–11)

Общий вид

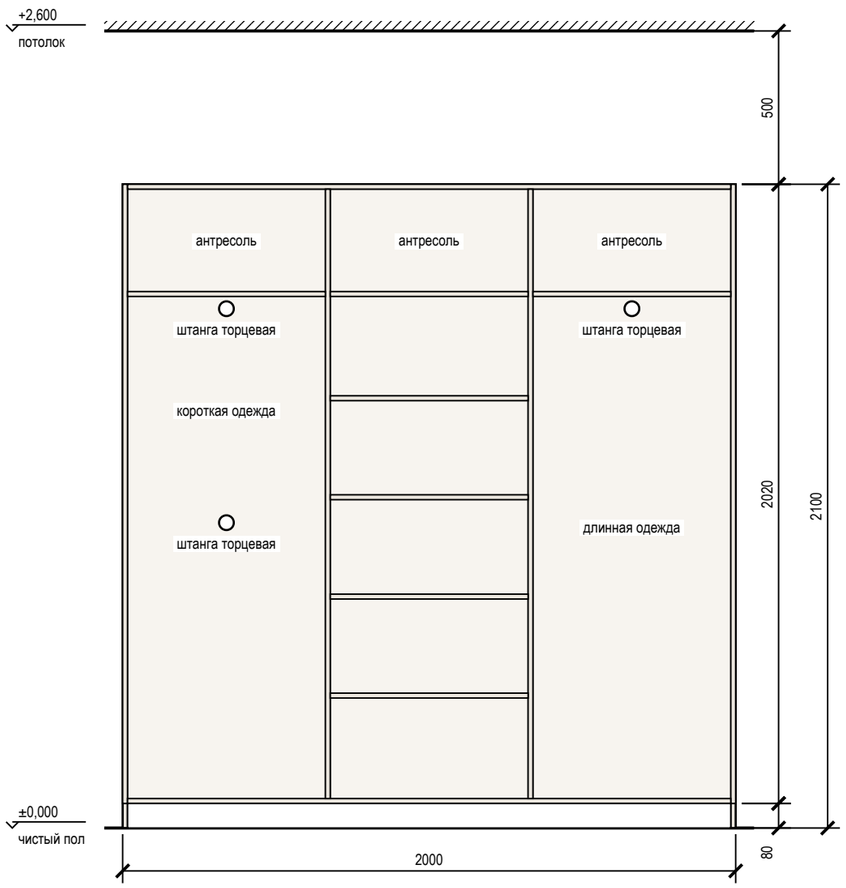

Наполнение, размеры в свету

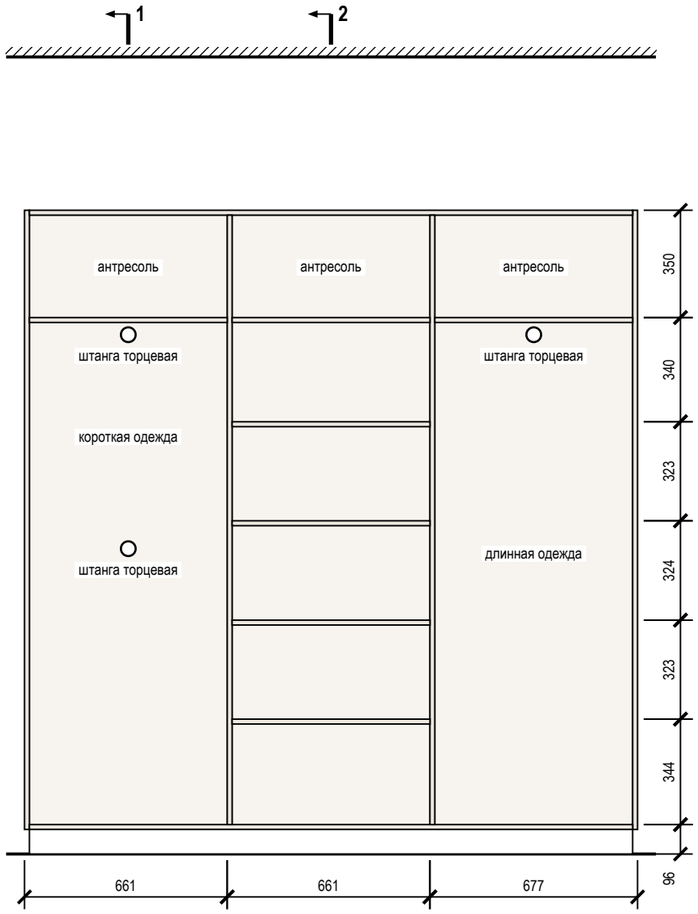

Разрез 1-1

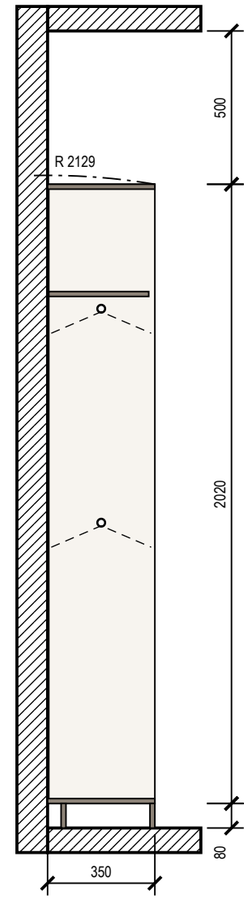

Разрез 2-2

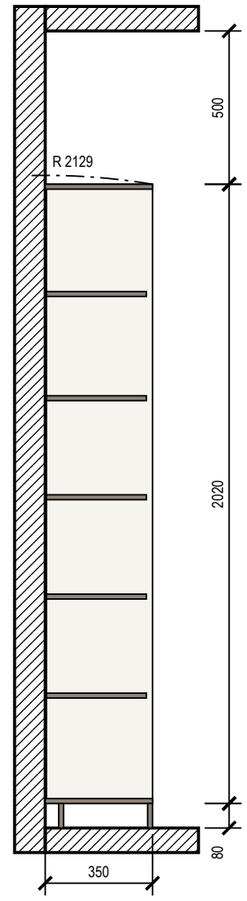

Примечания

1. Размеры — в мм по чистовой отделке; изделие 2000×350×2100 (Ш×Г×В). Перед раскроем — контрольный замер цеха после чистовой отделки стен, пола и потолка.
2. Корпус — ЛДСП 16 мм, задняя стенка ХДФ 4 мм в паз, цоколь 80 мм на регулируемых опорах; открытая система без фасадов, ящики с фасадами.
3. Кромка: скрытые торцы 0,4 мм, видимые 2 мм (ПВХ/АБС).
4. Номинальные зазоры: между фасадами ящиков 3 мм, фасад ящика — стойка 2 мм.
5. Ящики — направляющие полного выдвижения NL 300 (внутренняя глубина 346 мм ≥ NL + 3); присадка по 32-й системе — выполняет цех.
6. Зазор до потолка 500 мм.
7. Подъём корпуса: диагональ боковины $\sqrt{(2100^2 + 350^2)} = 2129$ мм < 2600 мм до потолка — корпус собирается лёжа и поднимается поворотом.
8. Крепление к стене от опрокидывания: крепление к стене, 3 точки; основание стены и шаг анкеров — монтажная схема шкафов.

Условные обозначения

- корпус и полки ЛДСП (вид на стену)
- задняя стенка ХДФ
- деталь в разрезе
- штанга для плечиков (на разрезе — плечики 450 мм)
- траектория угла корпуса при подъёме в проектное положение

Допущения и предложения на листе

Основа листа: размеры сняты с размерных цепочек растрового скана плана заказчика, на объекте не замерены; ступени наружного контура приведены к граням помещений модели (ИЗ-8, К-20, К-21); высота потолка 2700 мм принята, источника нет (К-24); тип дома и перекрытие (монолит, плита 220 мм) приняты, источника нет (К-3); толщины стен приняты (250 и 120 мм), источника нет (К-21); мощность 15 кВт принята, технических условий нет (К-25).
См. лист открытых вопросов (лист 6, запись К-3; лист 7, записи К-20, К-21, К-24, К-25; лист 10, запись ИЗ-8).

1000 мм · печать 1:1

Изм.	Кол.уч	Лист	№ док.	Подп.	Дата
Разраб.		Кырлан А.С.			21.10.26
Пров.					
ГИП		Кырлан А.С.			21.10.26
Н. контр.					
Утв.					

ГД-2026-004-АИ

Четырёхкомнатная квартира

Общая площадь 102,67* м² · * размеры со скана, не замерены (реестр — л. 6–11, ИЗ-8, К-20, К-21)

Дизайн-проект интерьера четырёхкомнатной квартиры

Стадия	Лист	Листов
РП	72	124

Система хранения M18

М 1:20

Кырлан Александр Сергеевич

выпуск 05.10.2026 № 7e7a2cd217 · стр. 82 из 168

Система хранения M19

Коридор (пом. 5) · вид из помещения · размеры в мм, отметки в м

ПРЕДВАРИТЕЛЬНО · не для производства работ · открыто пунктов: 30 (реестр — л. 6–11)

Вид с фасадами

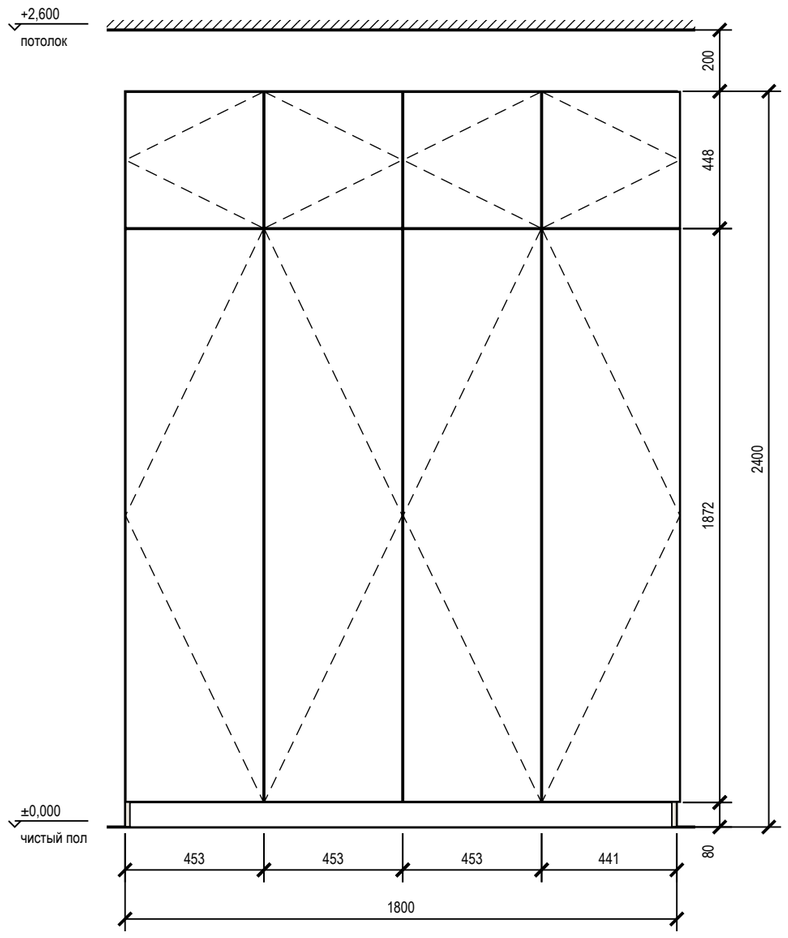

Вид без фасадов

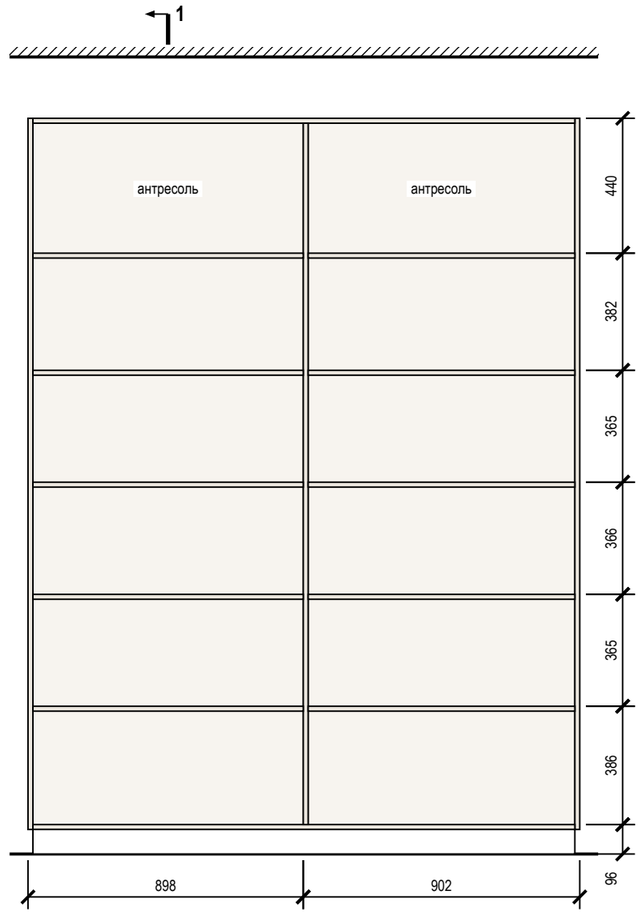

Разрез 1-1

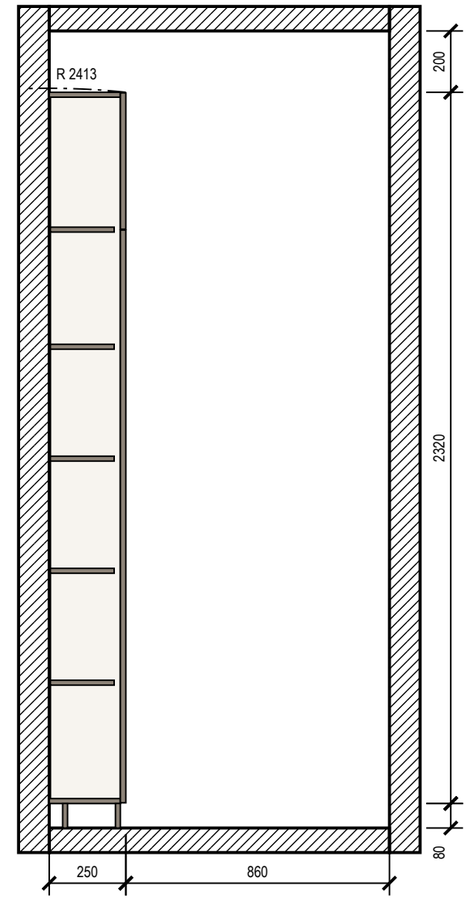

Примечания

1. Размеры — в мм по чистовой отделке; изделие 1800×250×2400 (Ш×Г×В). Перед раскроем — контрольный замер цеха после чистовой отделки стен, пола и потолка.
2. Корпус — ЛДСП 16 мм, задняя стенка ХДФ 4 мм в паз, цоколь 80 мм на регулируемых опорах; фасады — МДФ, эмаль матовая 18 мм накладные, цвет — по колерной карте; петли с доводчиком: фасад 1869 мм — 4 петли, фасад 445 мм — 2 петли.
3. Кромка: скрытые торцы 0,4 мм, видимые 2 мм (ПВХ/АБС).
4. Номинальные зазоры: между фасадами 3 мм, фасад — стена и фасад — потолок не менее 3 мм, фасад ящика — стойка 2 мм.
5. Присадка по 32-й системе — выполняет цех.
6. Зазор до потолка 200 мм.
7. Подъём корпуса: диагональ боковины $\sqrt{(2400^2 + 250^2)} = 2413$ мм < 2600 мм до потолка — корпус собирается лёжа и поднимается поворотом.
8. Крепление к стене от опрокидывания: крепление к стене, 4 точки; основание стены и шаг анкеров — монтажная схема шкафов.
9. Проход перед изделием 860 мм показан на разрезе 1-1.

Условные обозначения

- фасад распашной: линии сходятся к стороне петель
- корпус и полки ЛДСП (вид на стену)
- задняя стенка ХДФ
- деталь в разрезе
- штанга для плечиков (на разрезе — плечики 450 мм)
- траектория угла корпуса при подъёме в проектное положение

Допущения и предложения на листе

Основа листа: размеры сняты с размерных цепочек растрового скана плана заказчика, на объекте не замерены; ступени наружного контура приведены к граням помещений модели (ИЗ-8, К-20, К-21); высота потолка 2700 мм принята, источника нет (К-24); тип дома и перекрытие (монолит, плита 220 мм) приняты, источника нет (К-3); толщины стен приняты (250 и 120 мм), источника нет (К-21); мощность 15 кВт принята, технических условий нет (К-25).
См. лист открытых вопросов (лист 6, запись К-3; лист 7, записи К-20, К-21, К-24, К-25; лист 10, запись ИЗ-8).

1000 мм · печать 1:1

Изм.	Кол.уч	Лист	№ док.	Подп.	Дата
Разраб.		Кырлан А.С.			21.10.26
Пров.					
ГИП		Кырлан А.С.			21.10.26
Н. контр.					
Утв.					

ГД-2026-004-АИ

Четырёхкомнатная квартира

Общая площадь 102,67* м² · * размеры со скана, не замерены (реестр — л. 6–11, ИЗ-8, К-20, К-21)

Дизайн-проект интерьера четырёхкомнатной квартиры

Стадия	Лист	Листов
РП	73	124

Система хранения M19

М 1:20

Кырлан Александр Сергеевич

выпуск 05.10.2026 № 7e7a2cd217 · стр. 83 из 168

Шкаф-купе М29

Прихожая-коридор (пом. 7) · вид из помещения · размеры в мм, отметки в м

ПРЕДВАРИТЕЛЬНО · не для производства работ · открыто пунктов: 30 (реестр — л. 6–11)

Вид с фасадами

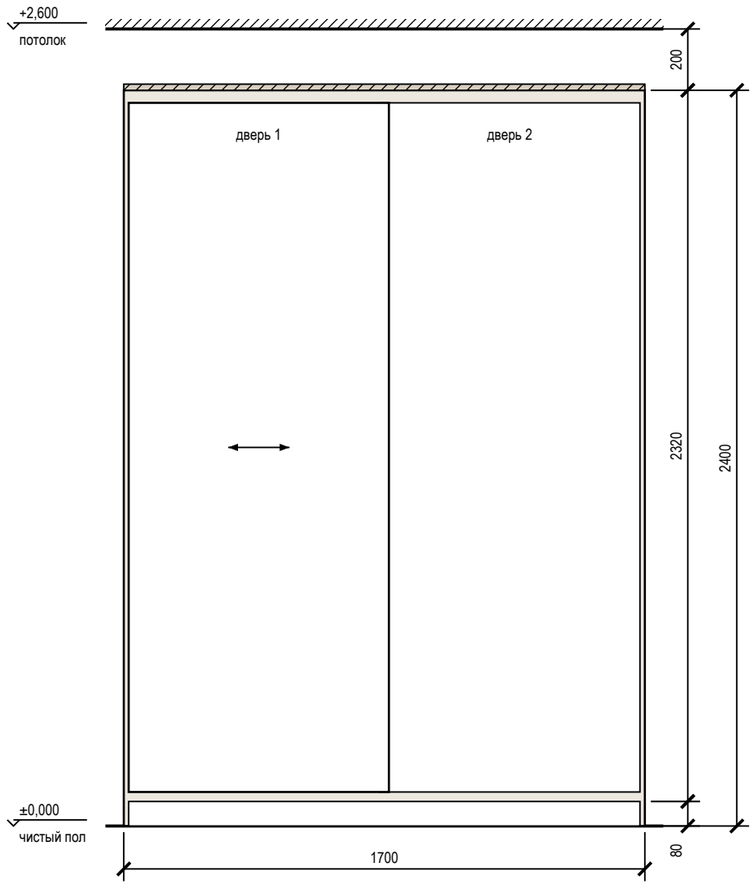

Вид без фасадов

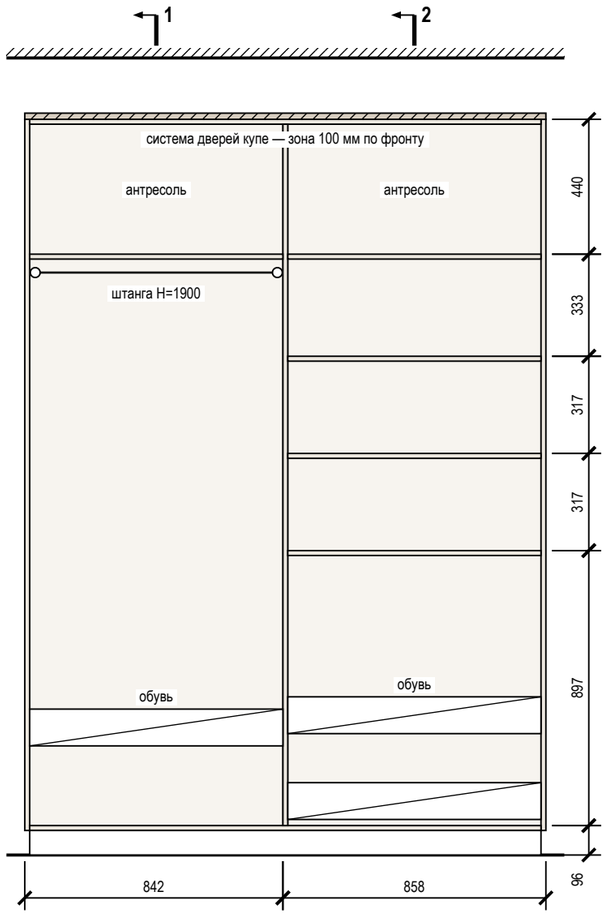

Разрез 1-1

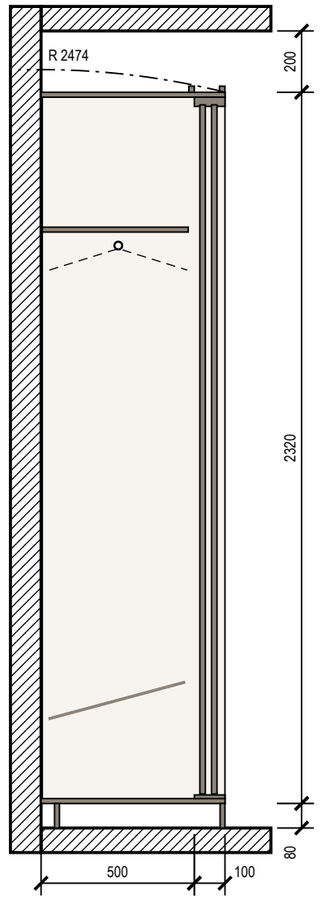

Разрез 2-2

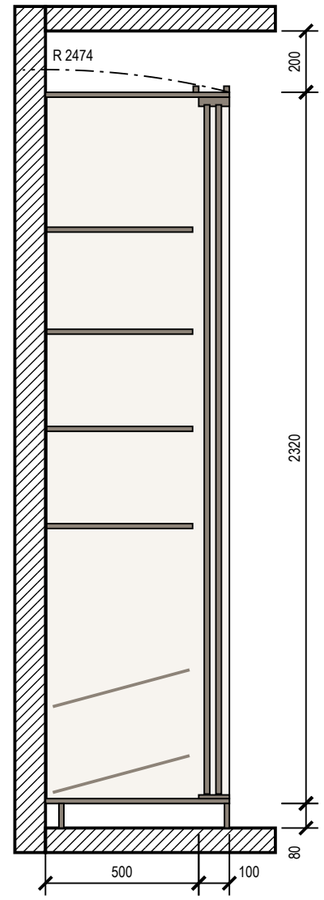

Примечания

1. Размеры — в мм по чистовой отделке; изделие 1700×600×2400 (Ш×Г×В). Перед раскроем — контрольный замер цеха после чистовой отделки стен, пола и потолка.
2. Корпус — ЛДСП 16 мм, задняя стенка ХДФ 4 мм в паз, цоколь 80 мм на регулируемых опорах; двери купе — ЛДСП 10 мм в алюминиевом профиле, нахлёст 30 мм, ширина двери 849 мм, высота — проём минус 40 мм; цвет — по колерной карте.
3. Кромка: скрытые торцы 0,4 мм, видимые 2 мм (ПВХ/АБС).
4. Номинальные зазоры: дверь купе — боковина 3 мм, фасад ящика — стойка 2 мм; ящики внутри купе — с накладкой 30 мм на стойке со стороны нахлёста дверей.
5. Ящики — направляющие полного выдвижения NL 450 (внутренняя глубина 496 мм ≥ NL + 3); присадка по 32-й системе — выполняет цех.
6. Компенсатор 20 мм — короб из ЛДСП по фронту и торцам, подгоняется к потолку при монтаже (припуск 20 мм), крепится к корпусу и к потолку.
7. Подъём корпуса: диагональ боковины $\sqrt{(2400^2 + 600^2)} = 2474$ мм < 2600 мм до потолка — корпус собирается лёжа и поднимается поворотом.
8. Крепление к стене от опрокидывания: крепление к стене, 3 точки; основание стены и шаг анкеров — монтажная схема шкафов.

Условные обозначения

- дверь купе, стрелка — направление движения
- корпус и полки ЛДСП (вид на стену)
- задняя стенка ХДФ
- деталь в разрезе
- компенсатор — короб до потолка
- штанга для плечиков (на разрезе — плечики 450 мм)
- траектория угла корпуса при подъёме в проектное положение

Допущения и предложения на листе

Основа листа: размеры сняты с размерных цепочек растрового скана плана заказчика, на объекте не замерены; ступени наружного контура приведены к граням помещений модели (ИЗ-8, К-20, К-21); высота потолка 2700 мм принята, источника нет (К-24); тип дома и перекрытие (монолит, плита 220 мм) приняты, источника нет (К-3); толщины стен приняты (250 и 120 мм), источника нет (К-21); мощность 15 кВт принята, технических условий нет (К-25).
См. лист открытых вопросов (лист 6, запись К-3; лист 7, записи К-20, К-21, К-24, К-25; лист 10, запись ИЗ-8).

1000 мм · печать 1:1

Изм.	Кол.уч	Лист	№ док.	Подп.	Дата
Разраб.		Кырлан А.С.			21.10.26
Пров.					
ГИП		Кырлан А.С.			21.10.26
Н. контр.					
Утв.					

ГД-2026-004-АИ

Четырёхкомнатная квартира

Общая площадь 102,67* м² · * размеры со скана, не замерены (реестр — л. 6–11, ИЗ-8, К-20, К-21)

Дизайн-проект интерьера четырёхкомнатной квартиры

Стадия	Лист	Листов
РП	74	124

Шкаф-купе М29

М 1:20

Кырлан Александр Сергеевич

выпуск 05.10.2026 № 7e7a2cd217 · стр. 84 из 168

Система хранения M32

Гардеробная 2 (пом. 8) · вид из помещения · размеры в мм, отметки в м

ПРЕДВАРИТЕЛЬНО · не для производства работ · открыто пунктов: 30 (реестр — л. 6–11)

Общий вид

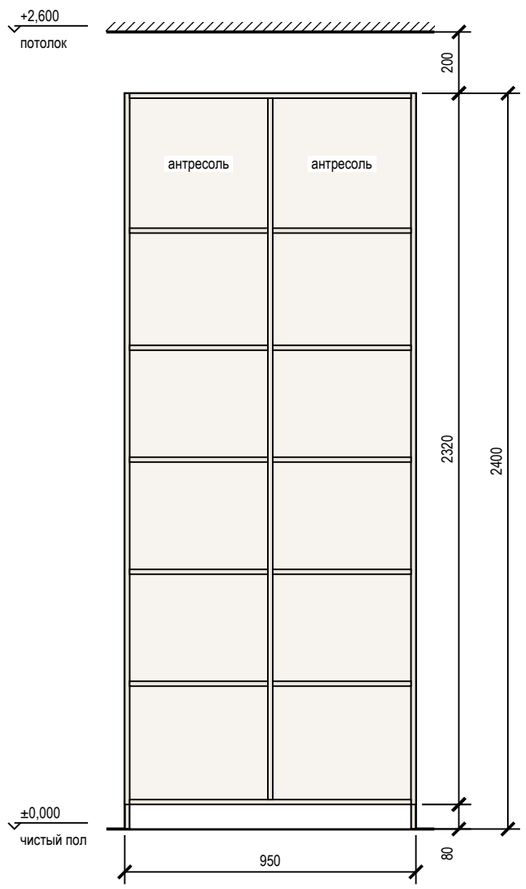

Наполнение, размеры в свету

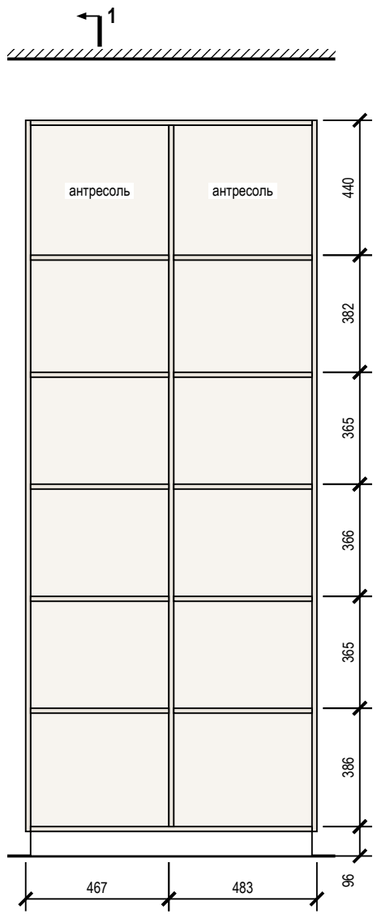

Разрез 1-1

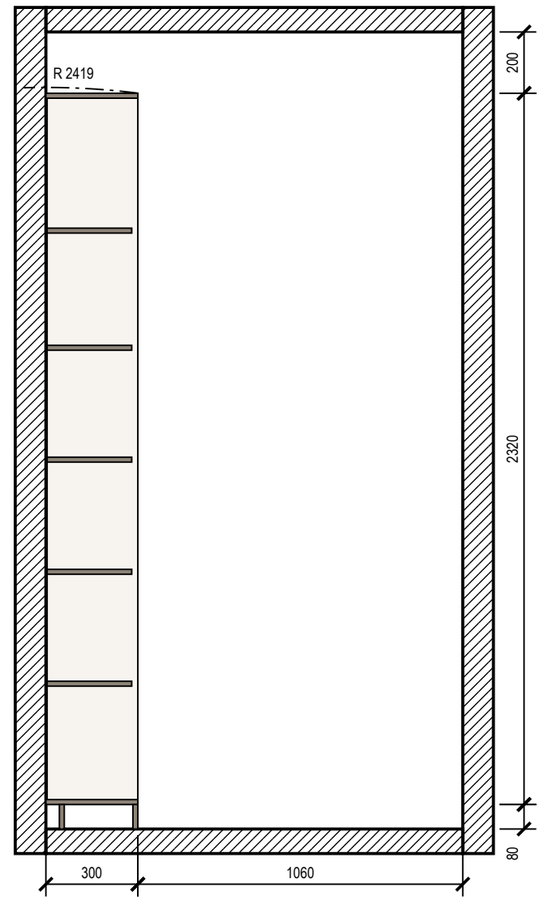

Примечания

1. Размеры — в мм по чистовой отделке; изделие 950×300×2400 (Ш×Г×В). Перед раскроем — контрольный замер цеха после чистовой отделки стен, пола и потолка.
2. Корпус — ЛДСП 16 мм, задняя стенка ХДФ 4 мм в паз, цоколь 80 мм на регулируемых опорах; открытая система без фасадов, ящики с фасадами.
3. Кромка: скрытые торцы 0,4 мм, видимые 2 мм (ПВХ/АБС).
4. Номинальные зазоры: между фасадами ящиков 3 мм, фасад ящика — стойка 2 мм.
5. Ящики — направляющие полного выдвижения NL 270 (внутренняя глубина 296 мм ≥ NL + 3); присадка по 32-й системе — выполняет цех.
6. Зазор до потолка 200 мм.
7. Подъём корпуса: диагональ боковины $\sqrt{(2400^2 + 300^2)}$ = 2419 мм < 2600 мм до потолка — корпус собирается лёжа и поднимается поворотом.
8. Крепление к стене от опрокидывания: крепление к стене, 3 точки; основание стены и шаг анкеров — монтажная схема шкафов.
9. Проход перед изделием 1060 мм показан на разрезе 1-1.

Условные обозначения

- корпус и полки ЛДСП (вид на стену)
- задняя стенка ХДФ
- деталь в разрезе
- штанга для плечиков (на разрезе — плечики 450 мм)
- траектория угла корпуса при подъёме в проектное положение

Допущения и предложения на листе

Основа листа: размеры сняты с размерных цепочек растрового скана плана заказчика, на объекте не замерены; ступени наружного контура приведены к граням помещений модели (ИЗ-8, К-20, К-21); высота потолка 2700 мм принята, источника нет (К-24); тип дома и перекрытие (монолит, плита 220 мм) приняты, источника нет (К-3); толщины стен приняты (250 и 120 мм), источника нет (К-21); мощность 15 кВт принята, технических условий нет (К-25).
См. лист открытых вопросов (лист 6, запись К-3; лист 7, записи К-20, К-21, К-24, К-25; лист 10, запись ИЗ-8).

1000 мм · печать 1:1

Изм.	Кол.уч	Лист	№ док.	Подп.	Дата
Разраб.		Кырлан А.С.			21.10.26
Пров.					
ГИП		Кырлан А.С.			21.10.26
Н. контр.					
Утв.					

ГД-2026-004-АИ

Четырёхкомнатная квартира

Общая площадь 102,67* м² · * размеры со скана, не замерены (реестр — л. 6–11, ИЗ-8, К-20, К-21)

Дизайн-проект интерьера четырёхкомнатной квартиры

Стадия	Лист	Листов
РП	75	124

Система хранения M32

М 1:20

Кырлан Александр Сергеевич

выпуск 05.10.2026 № 7e7a2cd217 · стр. 85 из 168

Система хранения М33

Гардеробная 2 (пом. 8) · вид из помещения · размеры в мм, отметки в м

Общий вид

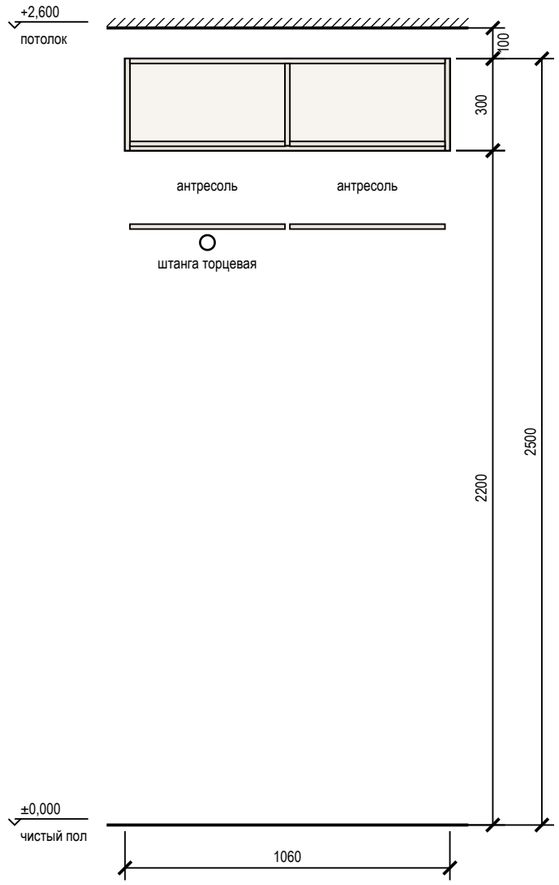

Наполнение, размеры в свету

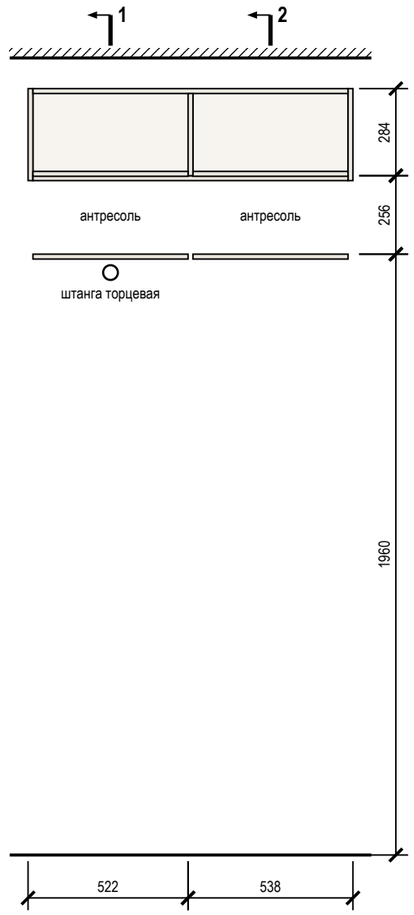

Разрез 1-1

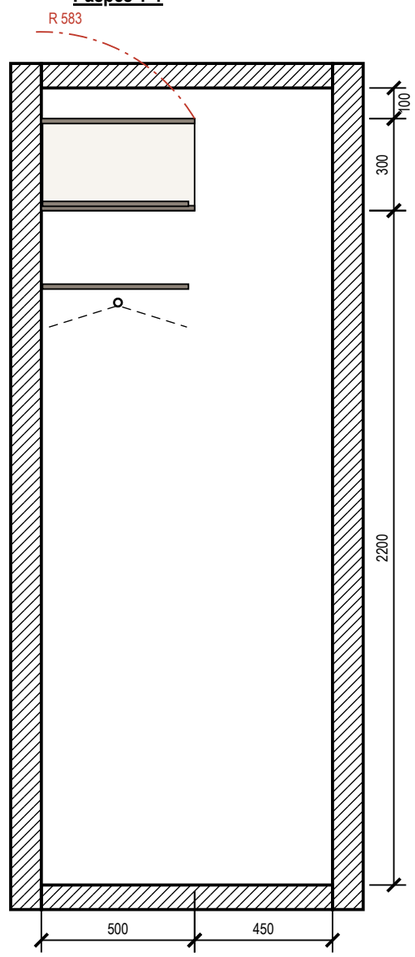

Разрез 2-2

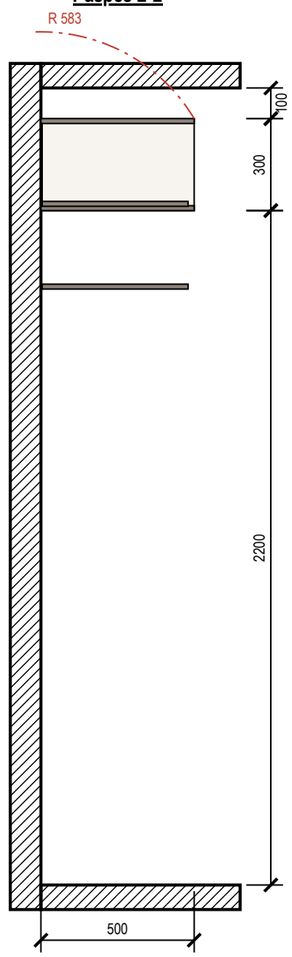

Примечания

1. Размеры — в мм по чистовой отделке; изделие 1060×500×300 (Ш×Г×В). Перед раскроем — контрольный замер цеха после чистовой отделки стен, пола и потолка.
2. Корпус — ЛДСП 16 мм, задняя стенка ХДФ 4 мм в паз, цоколь 0 мм на регулируемых опорах; открытая система без фасадов, ящики с фасадами.
3. Кромка: скрытые торцы 0,4 мм, видимые 2 мм (ПВХ/АБС).
4. Номинальные зазоры: между фасадами ящиков 3 мм, фасад ящика — стойка 2 мм.
5. Ящики — направляющие полного выдвижения NL 450 (внутренняя глубина 496 мм ≥ NL + 3); присадка по 32-й системе — выполняет цех.
6. Зазор до потолка 100 мм — закрыть планкой в цвет корпуса при монтаже.
7. Подъём корпуса (траектория на виде — красная: корпус не проходит под потолком): диагональ боковины $\sqrt{(300^2 + 500^2)} = 583$ мм > 400 мм до потолка — поднять собранный корпус нельзя: высота корпуса не более 0 мм, остальное — компенсатор, либо сборка стоя на месте.
8. Крепление к стене от опрокидывания: крепление к стене, 4 точки; основание стены и шаг анкеров — монтажная схема шкафов.
9. Проход перед изделием 450 мм показан на разрезе 1-1: меньше 600 мм — глубину уменьшить (торцевые штанги при глубине 350–450 мм) или изменить расстановку.

Условные обозначения

- корпус и полки ЛДСП (вид на стену)
- задняя стенка ХДФ
- деталь в разрезе
- штанга для плечиков (на разрезе — плечики 450 мм)
- траектория угла корпуса при подъёме в проектное положение

Допущения и предложения на листе

Основа листа: размеры сняты с размерных цепочек растрового скана плана заказчика, на объекте не замерены; ступени наружного контура приведены к граням помещений модели (ИЗ-8, К-20, К-21); высота потолка 2700 мм принята, источника нет (К-24); тип дома и перекрытие (монолит, плита 220 мм) приняты, источника нет (К-3); толщины стен приняты (250 и 120 мм), источника нет (К-21); мощность 15 кВт принята, технических условий нет (К-25).
См. лист открытых вопросов (лист 6, запись К-3; лист 7, записи К-20, К-21, К-24, К-25; лист 10, запись ИЗ-8).

1000 мм · печать 1:1

Изм.	Кол.уч	Лист	№ док.	Подп.	Дата
Разраб.		Кырлан А.С.			21.10.26
Пров.					
ГИП		Кырлан А.С.			21.10.26
Н. контр.					
Утв.					

ГД-2026-004-АИ

Четырёхкомнатная квартира

Общая площадь 102,67* м² · * размеры со скана, не замерены (реестр — л. 6–11, ИЗ-8, К-20, К-21)

Дизайн-проект интерьера четырёхкомнатной квартиры

Стадия	Лист	Листов
РП	76	124

Система хранения М33

М 1:20

Кырлан Александр Сергеевич

выпуск 05.10.2026 № 7e7a2cd217 · стр. 86 из 168

Шкаф распашной М35

Детская 2 (пом. 9) · вид из помещения · размеры в мм, отметки в м

ПРЕДВАРИТЕЛЬНО · не для производства работ · открыто пунктов: 30 (реестр — л. 6–11)

Вид с фасадами

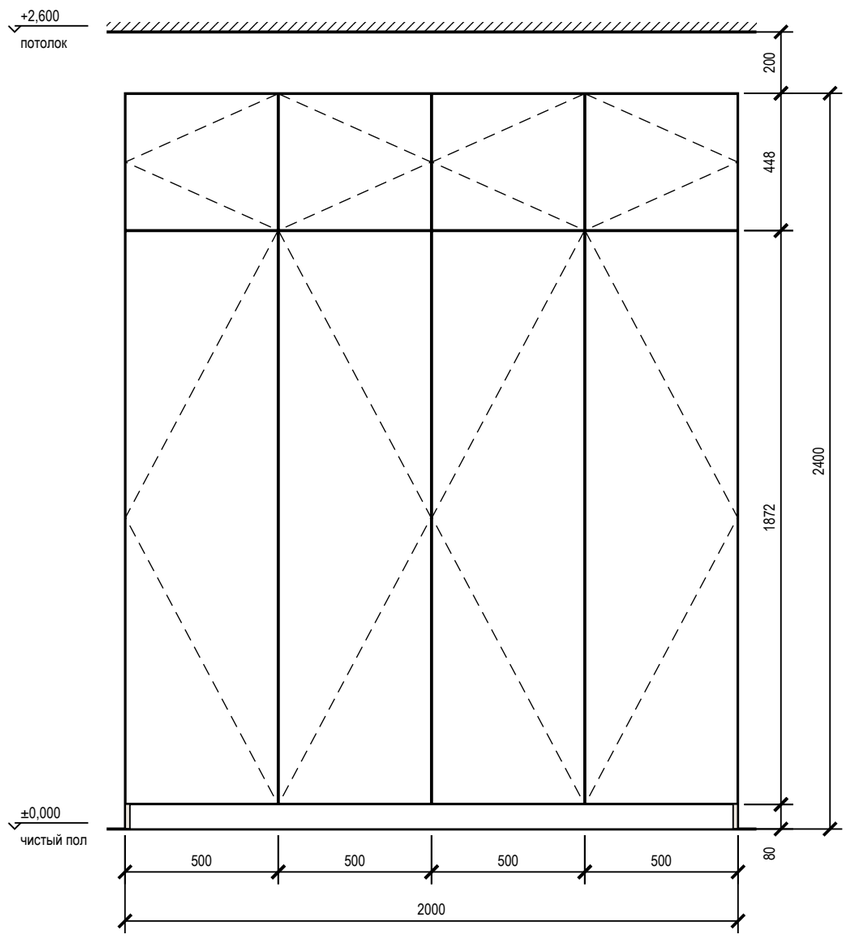

Вид без фасадов

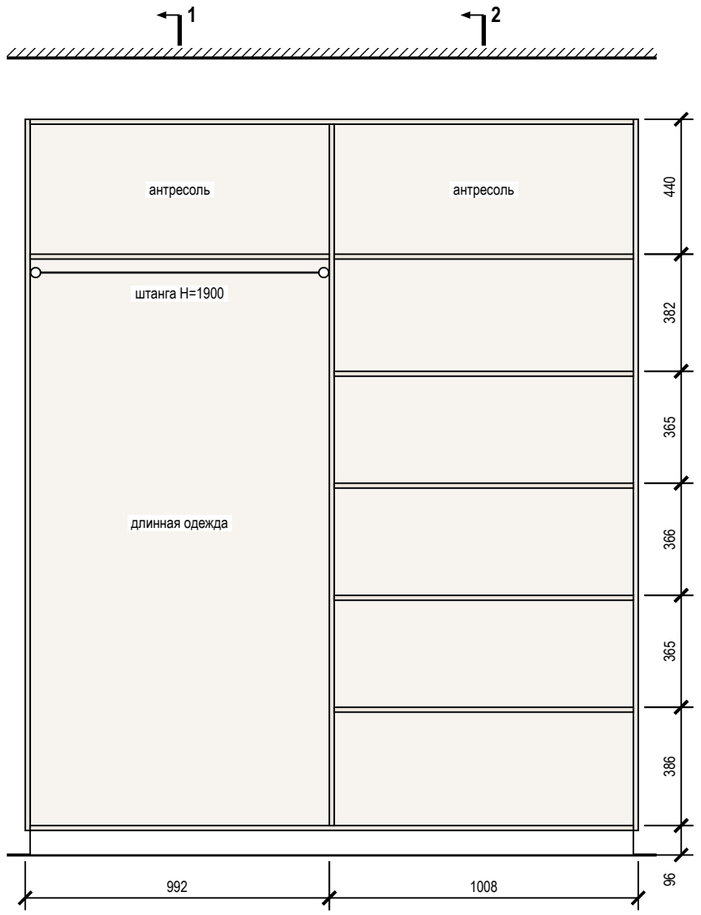

Разрез 1-1

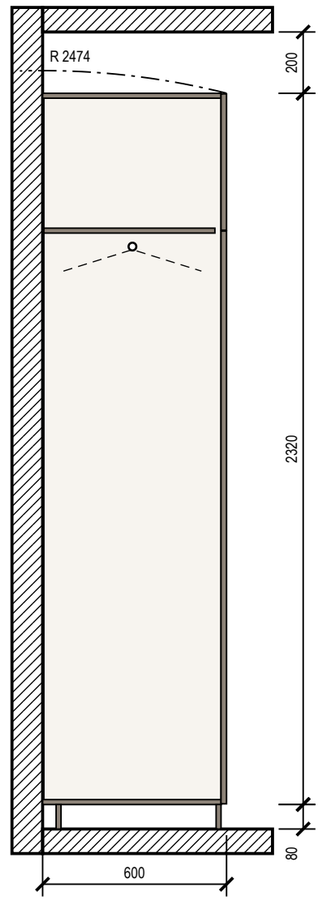

Разрез 2-2

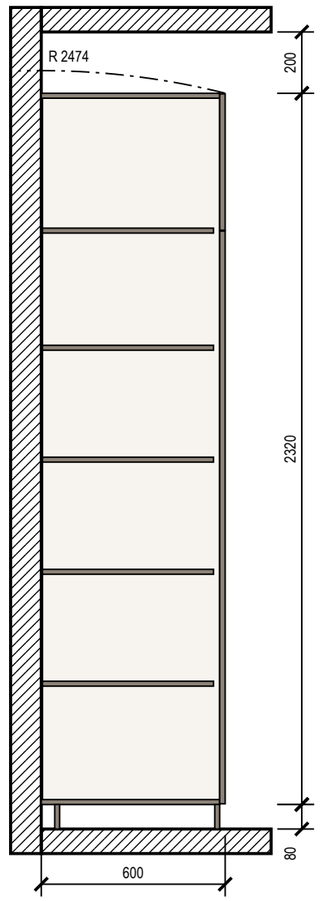

Примечания

1. Размеры — в мм по чистовой отделке; изделие 2000×600×2400 (Ш×Г×В). Перед раскроем — контрольный замер цеха после чистовой отделки стен, пола и потолка.
2. Корпус — ЛДСП 16 мм, задняя стенка ХДФ 4 мм в паз, цоколь 80 мм на регулируемых опорах; фасады — МДФ, эмаль матовая 18 мм накладные, цвет — по колерной карте; петли с доводчиком: фасад 1869 мм — 4 петли, фасад 445 мм — 2 петли.
3. Кромка: скрытые торцы 0,4 мм, видимые 2 мм (ПВХ/АБС).
4. Номинальные зазоры: между фасадами 3 мм, фасад — стена и фасад — потолок не менее 3 мм, фасад ящика — стойка 2 мм.
5. Ящики — направляющие полного выдвижения NL 550 (внутренняя глубина 578 мм ≥ NL + 3); присадка по 32-й системе — выполняет цех.
6. Зазор до потолка 200 мм.
7. Подъём корпуса: диагональ боковины $\sqrt{(2400^2 + 600^2)} = 2474$ мм < 2600 мм до потолка — корпус собирается лёжа и поднимается поворотом.
8. Крепление к стене от опрокидывания: уголок к стене, 3 шт.; основание стены и шаг анкеров — монтажная схема шкафов.

Условные обозначения

- фасад распашной: линии сходятся к стороне петель
- корпус и полки ЛДСП (вид на стену)
- задняя стенка ХДФ
- деталь в разрезе
- штанга для плечиков (на разрезе — плечики 450 мм)
- траектория угла корпуса при подъёме в проектное положение

Допущения и предложения на листе

Основа листа: размеры сняты с размерных цепочек растрового скана плана заказчика, на объекте не замерены; ступени наружного контура приведены к граням помещений модели (ИЗ-8, К-20, К-21); высота потолка 2700 мм принята, источника нет (К-24); тип дома и перекрытие (монолит, плита 220 мм) приняты, источника нет (К-3); толщины стен приняты (250 и 120 мм), источника нет (К-21); мощность 15 кВт принята, технических условий нет (К-25).

См. лист открытых вопросов (лист 6, запись К-3; лист 7, записи К-20, К-21, К-24, К-25; лист 10, запись ИЗ-8).

1000 мм · печать 1:1

Изм.	Кол.уч	Лист	№ док.	Подп.	Дата
Разраб.		Кырлан А.С.			21.10.26
Пров.					
ГИП		Кырлан А.С.			21.10.26
Н. контр.					
Утв.					

ГД-2026-004-АИ

Четырёхкомнатная квартира

Общая площадь 102,67* м² · * размеры со скана, не замерены (реестр — л. 6–11, ИЗ-8, К-20, К-21)

Дизайн-проект интерьера четырёхкомнатной квартиры

Стадия	Лист	Листов
РП	77	124

Шкаф распашной М35

М 1:20

Кырлан Александр Сергеевич

выпуск 05.10.2026 № 7e7a2cd217 · стр. 87 из 168

Система хранения М39

Гардеробная 1 (пом. 12) · вид из помещения · размеры в мм, отметки в м

ПРЕДВАРИТЕЛЬНО · не для производства работ · открыто пунктов: 30 (реестр — л. 6–11)

Общий вид

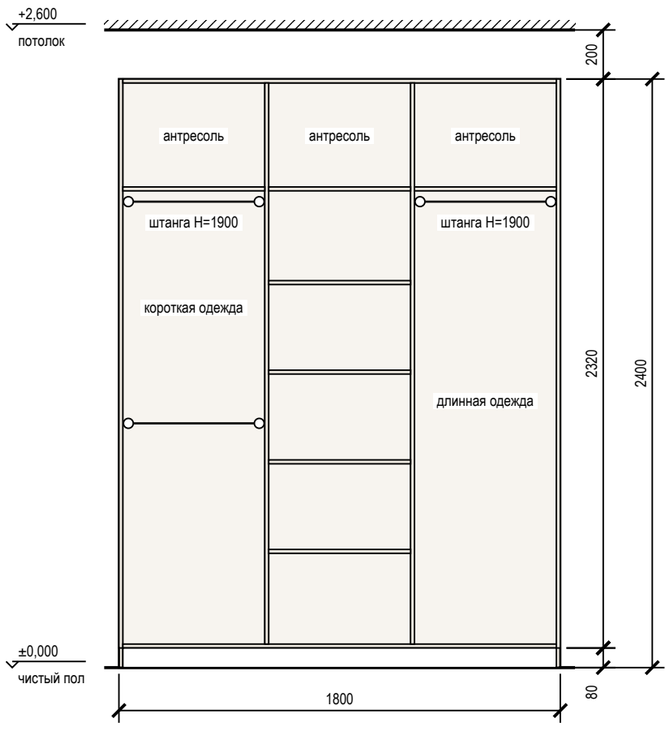

Наполнение, размеры в свету

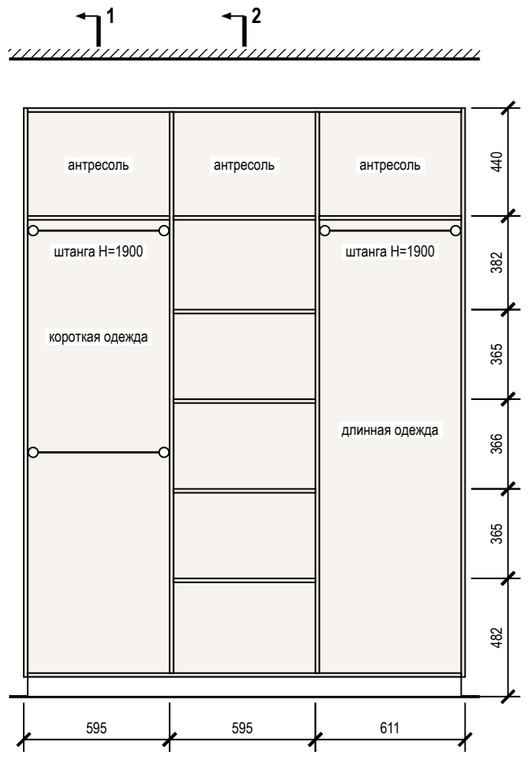

Разрез 1-1

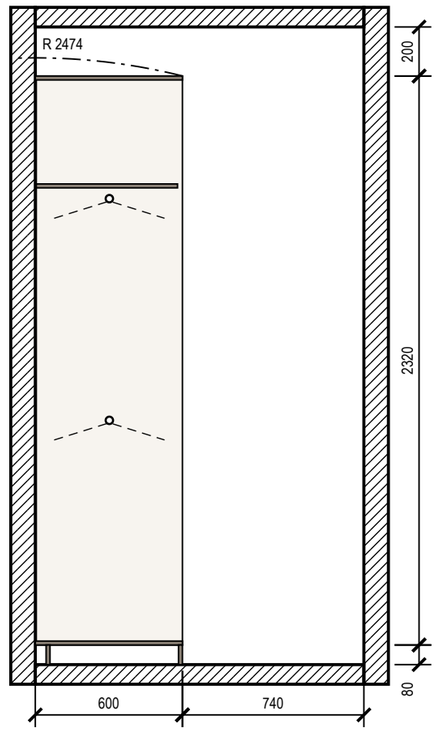

Разрез 2-2

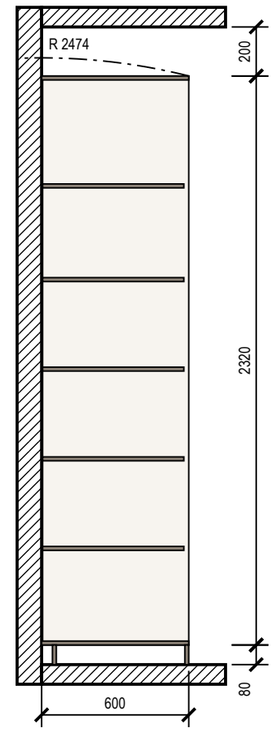

Примечания

1. Размеры — в мм по чистовой отделке; изделие 1800×600×2400 (Ш×Г×В). Перед раскроем — контрольный замер цеха после чистовой отделки стен, пола и потолка.
2. Корпус — ЛДСП 16 мм, задняя стенка ХДФ 4 мм в паз, цоколь 80 мм на регулируемых опорах; открытая система без фасадов, ящики с фасадами.
3. Кромка: скрытые торцы 0,4 мм, видимые 2 мм (ПВХ/АБС).
4. Номинальные зазоры: между фасадами ящиков 3 мм, фасад ящика — стойка 2 мм.
5. Ящики — направляющие полного выдвижения NL 550 (внутренняя глубина 596 мм ≥ NL + 3); присадка по 32-й системе — выполняет цех.
6. Зазор до потолка 200 мм.
7. Подъём корпуса: диагональ боковины $\sqrt{(2400^2 + 600^2)} = 2474$ мм < 2600 мм до потолка — корпус собирается лёжа и поднимается поворотом.
8. Крепление к стене от опрокидывания: крепление к стене, 4 точки; основание стены и шаг анкеров — монтажная схема шкафов.
9. Проход перед изделием 740 мм показан на разрезе 1-1.

Условные обозначения

- корпус и полки ЛДСП (вид на стену)
- задняя стенка ХДФ
- деталь в разрезе
- штанга для плечиков (на разрезе — плечики 450 мм)
- траектория угла корпуса при подъёме в проектное положение

Допущения и предложения на листе

Основа листа: размеры сняты с размерных цепочек растрового скана плана заказчика, на объекте не замерены; ступени наружного контура приведены к граням помещений модели (ИЗ-8, К-20, К-21); высота потолка 2700 мм принята, источника нет (К-24); тип дома и перекрытие (монолит, плита 220 мм) приняты, источника нет (К-3); толщины стен приняты (250 и 120 мм), источника нет (К-21); мощность 15 кВт принята, технических условий нет (К-25).

См. лист открытых вопросов (лист 6, запись К-3; лист 7, записи К-20, К-21, К-24, К-25; лист 10, запись ИЗ-8).

1000 мм · печать 1:1

Изм.	Кол.уч	Лист	№ док.	Подп.	Дата
Разраб.		Кырлан А.С.			21.10.26
Пров.					
ГИП		Кырлан А.С.			21.10.26
Н. контр.					
Утв.					

ГД-2026-004-АИ

Четырёхкомнатная квартира

Общая площадь 102,67* м² · * размеры со скана, не замерены (реестр — л. 6–11, ИЗ-8, К-20, К-21)

Дизайн-проект интерьера четырёхкомнатной квартиры

Стадия	Лист	Листов
РП	78	124

Система хранения М39

М 1:25

Кырлан Александр Сергеевич

выпуск 05.10.2026 № 7e7a2cd217 · стр. 88 из 168

Система хранения М41

Балкон 1 (пом. 13) · вид из помещения · размеры в мм, отметки в м

ПРЕДВАРИТЕЛЬНО · не для производства работ · открыто пунктов: 30 (реестр — л. 6–11)

Общий вид

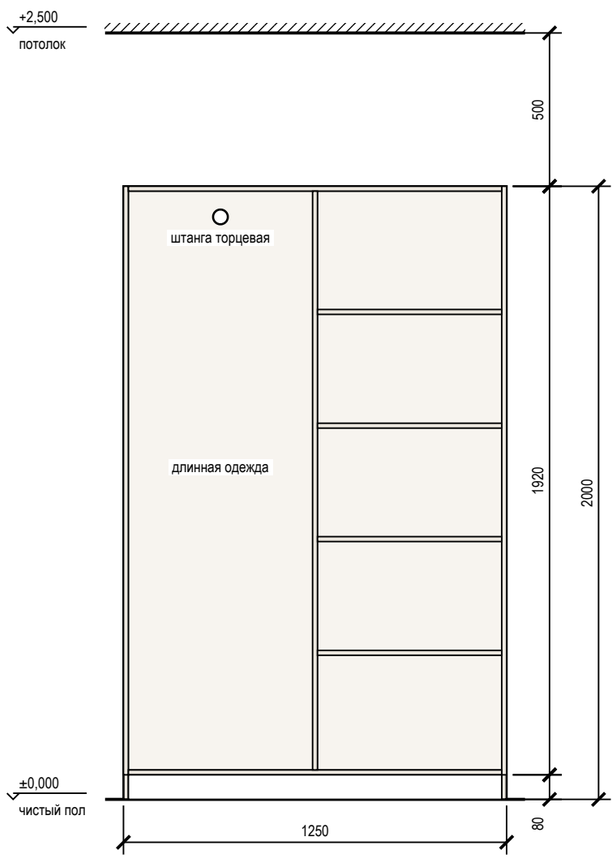

Наполнение, размеры в свету

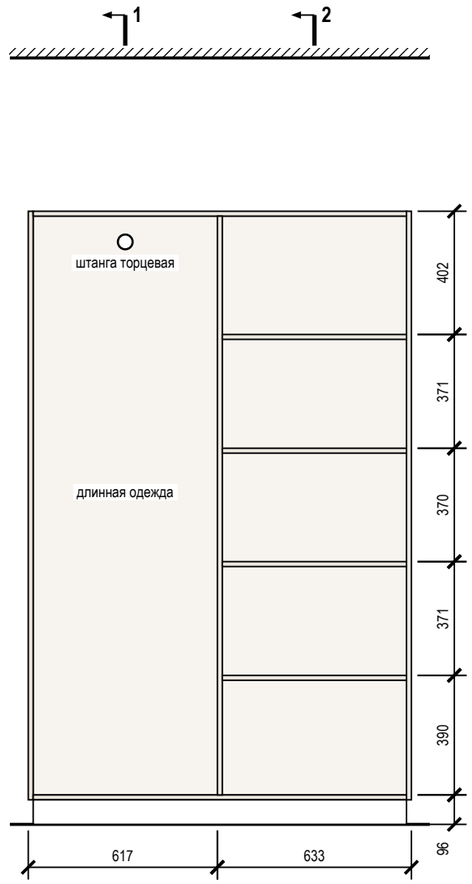

Разрез 1-1

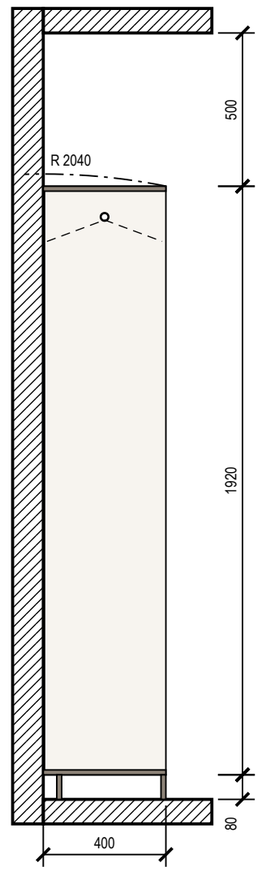

Разрез 2-2

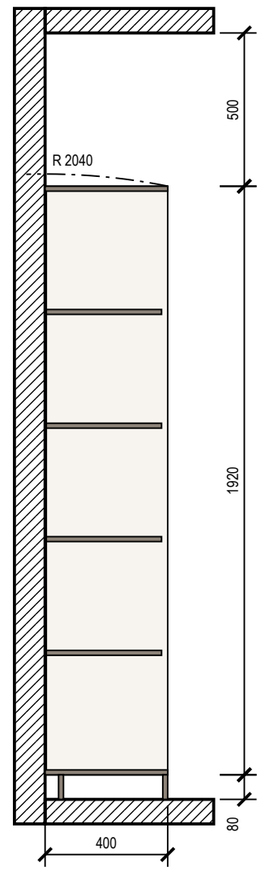

Примечания

1. Размеры — в мм по чистовой отделке; изделие 1250×400×2000 (Ш×Г×В). Перед раскроем — контрольный замер цеха после чистовой отделки стен, пола и потолка.
2. Корпус — ЛДСП 16 мм, задняя стенка ХДФ 4 мм в паз, цоколь 80 мм на регулируемых опорах; открытая система без фасадов, ящики с фасадами.
3. Кромка: скрытые торцы 0,4 мм, видимые 2 мм (ПВХ/АБС).
4. Номинальные зазоры: между фасадами ящиков 3 мм, фасад ящика — стойка 2 мм.
5. Ящики — направляющие полного выдвижения NL 350 (внутренняя глубина 396 мм ≥ NL + 3); присадка по 32-й системе — выполняет цех.
6. Зазор до потолка 500 мм.
7. Подъём корпуса: диагональ боковины $\sqrt{(2000^2 + 400^2)} = 2040$ мм < 2500 мм до потолка — корпус собирается лёжа и поднимается поворотом.
8. Крепление к стене от опрокидывания: крепление к стене, 3 точки; основание стены и шаг анкеров — монтажная схема шкафов.

Условные обозначения

- корпус и полки ЛДСП (вид на стену)
- задняя стенка ХДФ
- деталь в разрезе
- штанга для плечиков (на разрезе — плечики 450 мм)
- траектория угла корпуса при подъёме в проектное положение

Допущения и предложения на листе

Основа листа: размеры сняты с размерных цепочек растрового скана плана заказчика, на объекте не замерены; ступени наружного контура приведены к граням помещений модели (ИЗ-8, К-20, К-21); высота потолка 2700 мм принята, источника нет (К-24); тип дома и перекрытие (монолит, плита 220 мм) приняты, источника нет (К-3); толщины стен приняты (250 и 120 мм), источника нет (К-21); мощность 15 кВт принята, технических условий нет (К-25).
См. лист открытых вопросов (лист 6, запись К-3; лист 7, записи К-20, К-21, К-24, К-25; лист 10, запись ИЗ-8).

1000 мм · печать 1:1

Изм.	Кол.уч	Лист	№ док.	Подп.	Дата
Разраб.		Кырлан А.С.			21.10.26
Пров.					
ГИП		Кырлан А.С.			21.10.26
Н. контр.					
Утв.					

ГД-2026-004-АИ

Четырёхкомнатная квартира

Общая площадь 102,67* м² · * размеры со скана, не замерены (реестр — л. 6–11, ИЗ-8, К-20, К-21)

Дизайн-проект интерьера четырёхкомнатной квартиры

Стадия	Лист	Листов
РП	79	124

Система хранения М41

М 1:20

Кырлан Александр Сергеевич

выпуск 05.10.2026 № 7e7a2cd217 · стр. 89 из 168

Система хранения М42

Балкон 1 (пом. 13) · вид из помещения · размеры в мм, отметки в м

ПРЕДВАРИТЕЛЬНО · не для производства работ · открыто пунктов: 30 (реестр — л. 6–11)

Общий вид

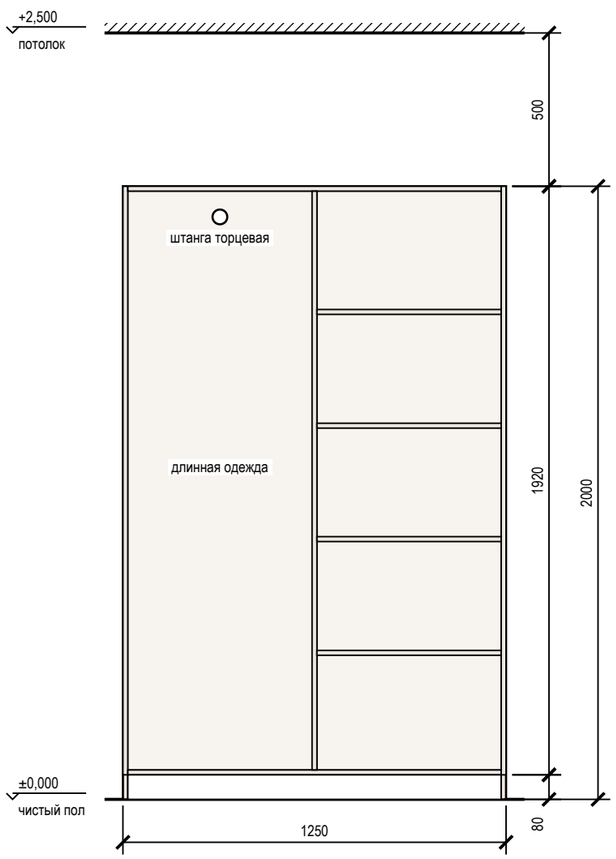

Наполнение, размеры в свету

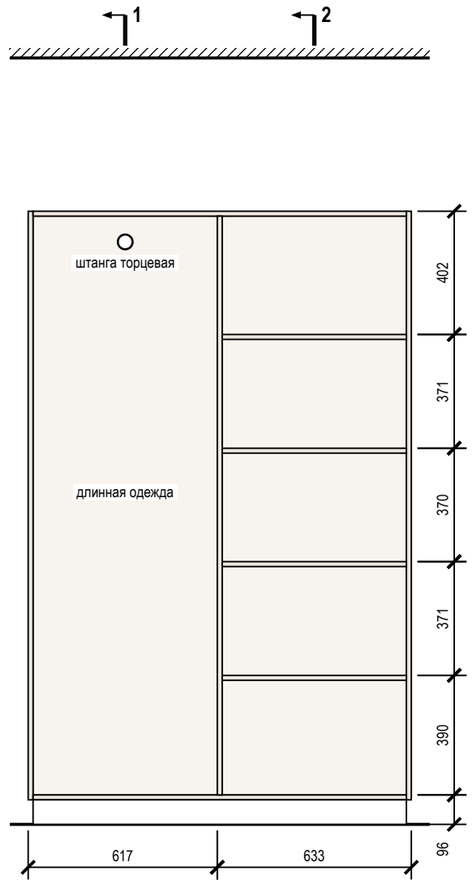

Разрез 1-1

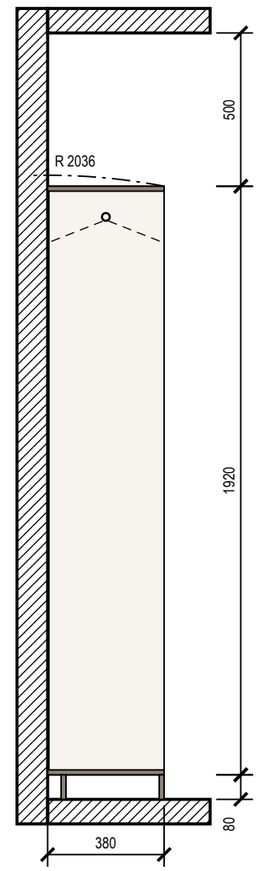

Разрез 2-2

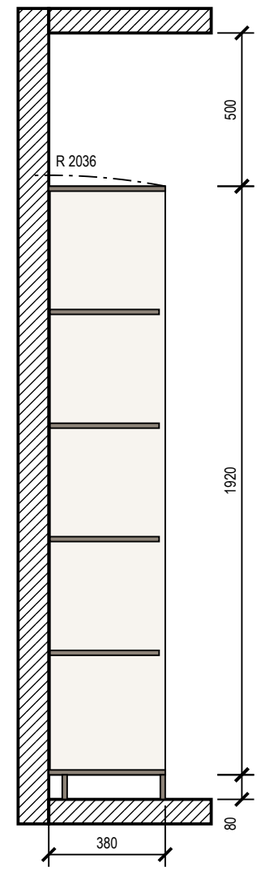

Примечания

1. Размеры — в мм по чистовой отделке; изделие 1250×380×2000 (Ш×Г×В). Перед раскроем — контрольный замер цеха после чистовой отделки стен, пола и потолка.
2. Корпус — ЛДСП 16 мм, задняя стенка ХДФ 4 мм в паз, цоколь 80 мм на регулируемых опорах; открытая система без фасадов, ящики с фасадами.
3. Кромка: скрытые торцы 0,4 мм, видимые 2 мм (ПВХ/АБС).
4. Номинальные зазоры: между фасадами ящиков 3 мм, фасад ящика — стойка 2 мм.
5. Ящики — направляющие полного выдвижения NL 350 (внутренняя глубина 376 мм ≥ NL + 3); присадка по 32-й системе — выполняет цех.
6. Зазор до потолка 500 мм.
7. Подъём корпуса: диагональ боковины $\sqrt{(2000^2 + 380^2)} = 2036$ мм < 2500 мм до потолка — корпус собирается лёжа и поднимается поворотом.
8. Крепление к стене от опрокидывания: крепление к стене, 3 точки; основание стены и шаг анкеров — монтажная схема шкафов.

Условные обозначения

- корпус и полки ЛДСП (вид на стену)
- задняя стенка ХДФ
- деталь в разрезе
- штанга для плечиков (на разрезе — плечики 450 мм)
- траектория угла корпуса при подъёме в проектное положение

Допущения и предложения на листе

Основа листа: размеры сняты с размерных цепочек растрового скана плана заказчика, на объекте не замерены; ступени наружного контура приведены к граням помещений модели (ИЗ-8, К-20, К-21); высота потолка 2700 мм принята, источника нет (К-24); тип дома и перекрытие (монолит, плита 220 мм) приняты, источника нет (К-3); толщины стен приняты (250 и 120 мм), источника нет (К-21); мощность 15 кВт принята, технических условий нет (К-25).
См. лист открытых вопросов (лист 6, запись К-3; лист 7, записи К-20, К-21, К-24, К-25; лист 10, запись ИЗ-8).

1000 мм · печать 1:1

Изм.	Кол.уч	Лист	№ док.	Подп.	Дата
Разраб.		Кырлан А.С.			21.10.26
Пров.					
ГИП		Кырлан А.С.			21.10.26
Н. контр.					
Утв.					

ГД-2026-004-АИ

Четырёхкомнатная квартира

Общая площадь 102,67* м² · * размеры со скана, не замерены (реестр — л. 6–11, ИЗ-8, К-20, К-21)

Дизайн-проект интерьера четырёхкомнатной квартиры

Стадия	Лист	Листов
РП	80	124

Система хранения М42

М 1:20

Кырлан Александр Сергеевич

выпуск 05.10.2026 № 7e7a2cd217 · стр. 90 из 168

Кухня (пом. 6). Развёртка гарнитура

Кухня (пом. 6) · стена А · вид из помещения · размеры в мм, отметки в м

Вид с фасадами

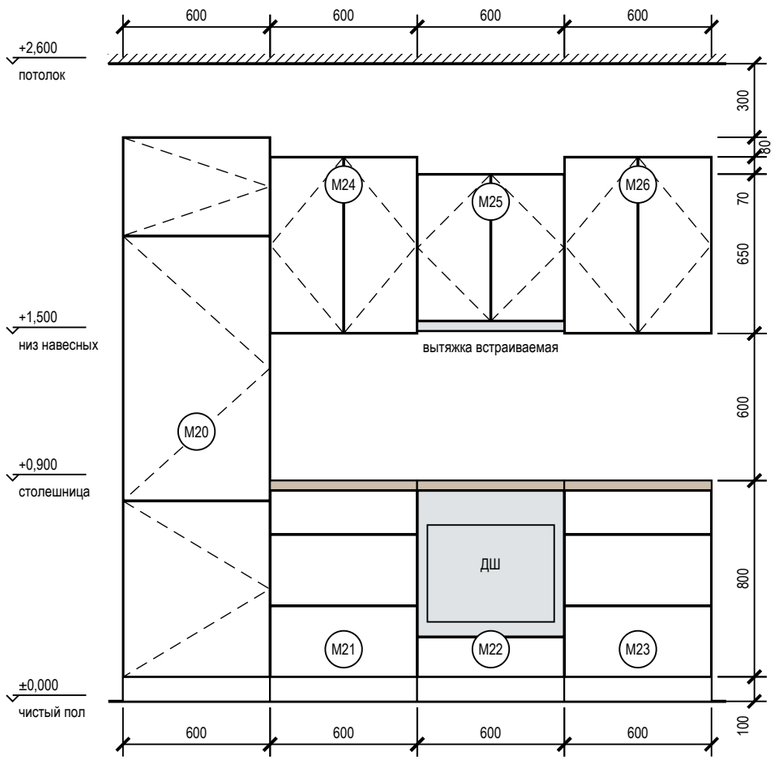

Вид без фасадов (наполнение, выводы)

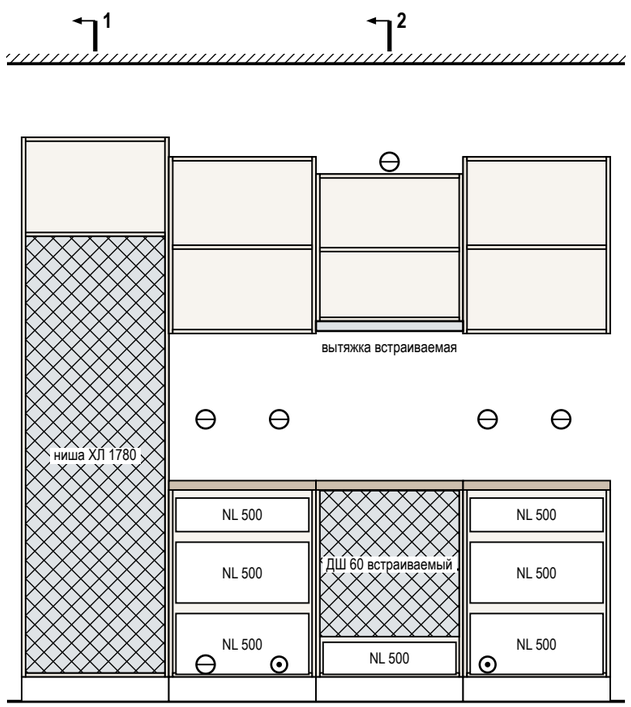

Разрез 1-1

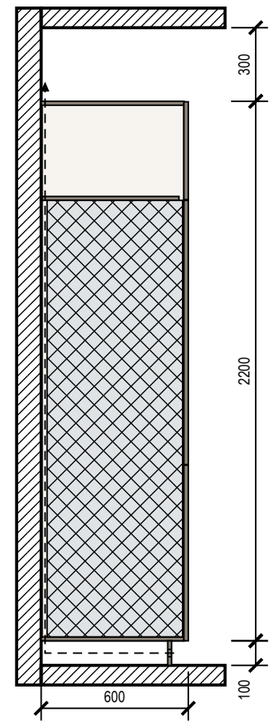

Разрез 2-2

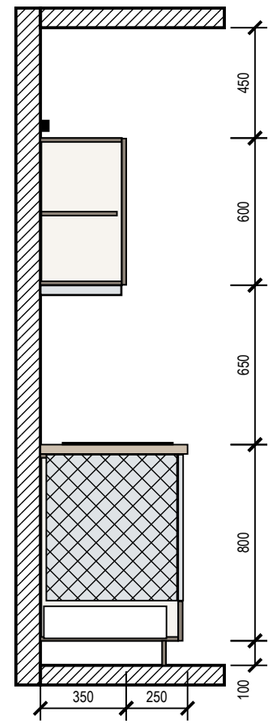

Условные обозначения

- фасад распашной: линии сходятся к стороне петель
- фасад ящика, карго
- встраиваемая техника
- столешница
- доборная планка
- деталь в разрезе
- К1 — марка модуля
- розетка на стене
- вывод кабеля к технике
- В1 — вывод воды В1 / Т3, канализации К1

Примечания

1. Размеры — в мм по чистовой отделке, вид из помещения; марки — как на плане расстановки. Перед раскроем — контрольный замер цеха после фартука и пола.
2. Корпуса — ЛДСП 16 мм, задняя стенка ХДФ 4 мм; фасады — МДФ, эмаль матовая 18 мм, цвет по колерной карте; столешница 38 мм, свес 20 мм; цоколь 100 мм.
3. Кромка: скрытые торцы 0,4 мм, видимые 2 мм. Номинальные зазоры: между фасадами 3 мм, фасад — столешница 3 мм, фасад — стена не менее 3 мм.
4. Ящики полного выдвижения и петли — с доводчиком; присадка по 32-й системе — выполняет цех.
5. Вытяжка встраивается в навесной модуль над варочной: её низ 610 мм над панелью — меньше 650 мм, модуль поднять или принять вытяжку с допуском по паспорту модели.
6. Ниши техники (холодильник — ориентир 1780 мм) — по монтажным схемам выбранных моделей: решётка в цоколе и канал за пеналом холодильника, зазор за духовым шкафом, фасад ПММ на двери машины.

Допущения и предложения на листе

Основа листа: размеры сняты с размерных цепочек растрового скана плана заказчика, на объекте не замерены; ступени наружного контура приведены к граням помещений модели (ИЗ-8, К-20, К-21); высота потолка 2700 мм принята, источника нет (К-24); тип дома и перекрытие (монолит, плита 220 мм) приняты, источника нет (К-3); толщины стен приняты (250 и 120 мм), источника нет (К-21); мощность 15 кВт принята, технических условий нет (К-25).

Открытые вопросы и конфликты по листу: К-18, К-27.

См. лист открытых вопросов (лист 6, запись К-3; лист 7, записи К-18, К-20, К-21, К-24, К-25; лист 8, запись К-27; лист 10, запись ИЗ-8).

1000 мм · печать 1:1

Изм.	Кол.уч	Лист	№ док.	Подп.	Дата
Разраб.		Кырлан А.С.			21.10.26
Пров.					
ГИП		Кырлан А.С.			21.10.26
Н. контр.					
Утв.					

ГД-2026-004-АИ

Четырёхкомнатная квартира

Общая площадь 102,67* м² · * размеры со скана, не замерены (реестр — л. 6–11, ИЗ-8, К-20, К-21)

Дизайн-проект интерьера четырёхкомнатной квартиры

Стадия	Лист	Листов
РП	81	124

Кухня (пом. 6). Развёртка гарнитура

М 1:25

Кырлан Александр Сергеевич

выпуск 05.10.2026 № 7e7a2cd217 · стр. 91 из 168

Кухня (пом. 6). Монтажная схема

Кухня (пом. 6) · стена А · размеры в мм от чистых поверхностей, высоты — от чистого пола

ПРЕДВАРИТЕЛЬНО · не для производства работ · открыто пунктов: 30 (реестр — л. 6–11)

Привязка выводов и крепление модулей

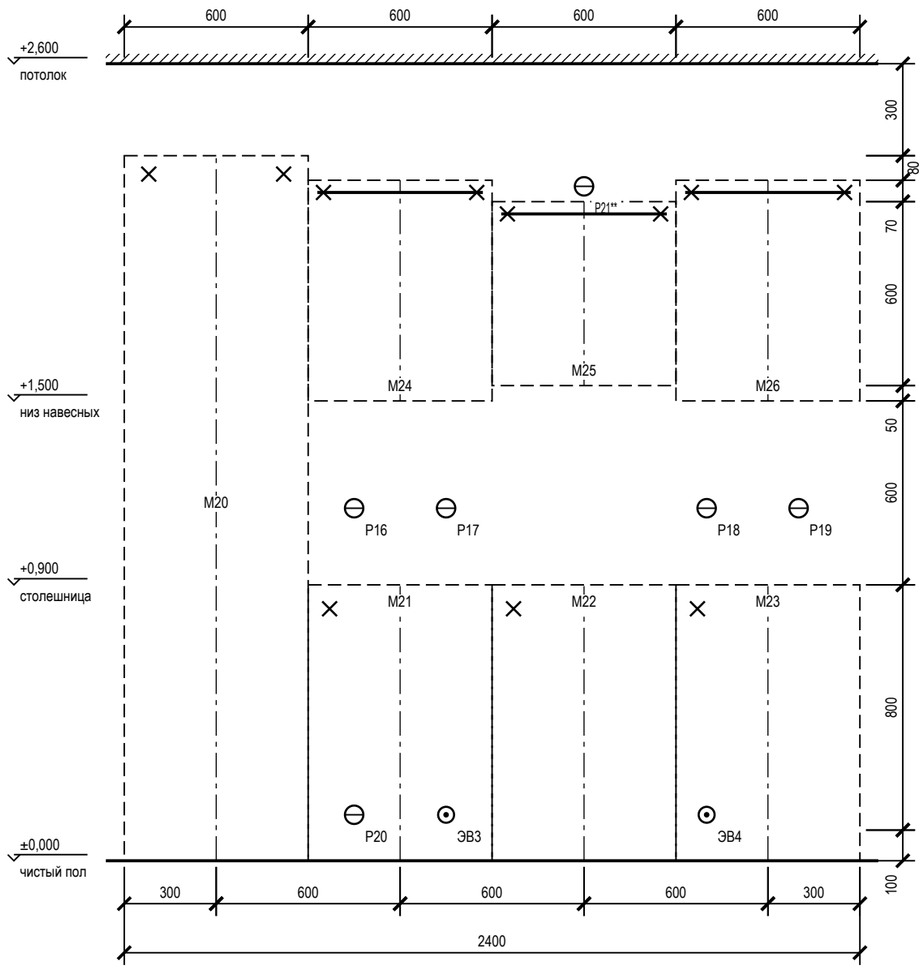

План столешницы

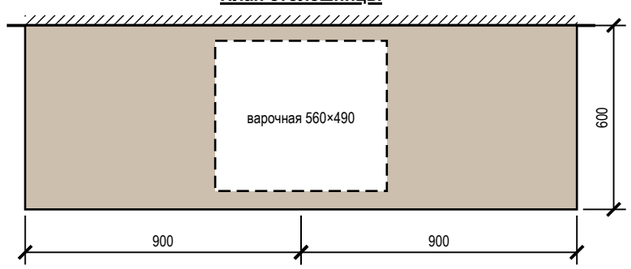

Привязка выводов к осям модулей

Код	Назначение	Модуль	От оси, мм	H, мм	Размещение
P16	розетка ×2 — фартук: мелкая техника	M21	−150	1150	над столешницей (фартук)
P20	розетка — холодильник встроенный M20 (розетка в модуле M21)	M21	−150	150	в соседнем модуле, за ящиком
P17	розетка ×2 — фартук: мелкая техника	M21	+150	1150	над столешницей (фартук)
ЭВ3	вывод кабеля — варочная панель M22	M21	+150	150	в соседнем модуле, за ящиком
P21**	розетка — вытяжка M25 (в модуле, съёмная панель)	M25	0	2200	в навесном модуле
P18	розетка ×2 — фартук: мелкая техника	M23	−200	1150	над столешницей (фартук)
ЭВ4	вывод кабеля — духовой шкаф M22 (вывод в соседнем модуле M23)	M23	−200	150	в соседнем модуле, за ящиком
P19	розетка ×2 — фартук: мелкая техника	M23	+100	1150	над столешницей (фартук)

Зазоры под отделку

Поверхность	Отделка	Зазор, мм	Учесть
фартук	керамогранит	10	от чернового основания до корпуса навесных и столешницы
стены	окраска	5	под штукатурку и шпаклёвку за пеналом
пол	инженерная доска		цоколь — после укладки пола, опоры ±20 мм

Условные обозначения

- навесной модуль (невидимый контур)
- ось модуля (от неё — привязка вывода)
- анкер / уголок крепления к стене
- розетка на стене
- вывод кабеля к технике
- B1 — вывод воды B1 / Т3, канализации К1

Допущения и предложения на листе

Основа листа: размеры сняты с размерных цепочек растрового скана плана заказчика, на объекте не замерены; ступени наружного контура приведены к граням помещений модели (ИЗ-8, К-20, К-21); высота потолка 2700 мм принята, источника нет (К-24); тип дома и перекрытие (монолит, плита 220 мм) приняты, источника нет (К-3); толщины стен приняты (250 и 120 мм), источника нет (К-21); мощность 15 кВт принята, технических условий нет (К-25).

Знак «**» — предложение проектировщика, заказчиком не утверждено (согласовать с заказчиком): ИЗ-10, К-23: P21 — высота 2200 мм выше нормы 1 м (ПУЭ 6.6.30) по назначению: питание вытяжки M25, розетка в модуле за съёмной панелью.

Открытые вопросы и конфликты по листу: К-14, К-27.

См. лист открытых вопросов (лист 6, запись К-3; лист 7, записи К-14, К-20, К-21, К-23–К-25; лист 8, запись К-27; лист 10, записи ИЗ-8, ИЗ-10).

Примечания

1. Выводы — по проекту электрики и ВК; привязка по горизонтали — от оси модуля (плюс — вправо по виду), по высоте — от чистого пола до оси вывода.
2. Пенал — уголки к стене 2 шт. сверху; нижние модули — стяжками между собой и уголком к стене; ряд выставить по уровню опорами цоколя.
3. Розетки над столешницей — не ниже 150 мм над ней и не за корпусом техники; розетка за ПММ, духовым шкафом и холодильником — только в соседнем модуле или в зоне цоколя с доступом.
4. Столешница — вырезы по шаблонам выбранных моделей мойки и варочной панели; торцы у стены — герметик, пристеночный плинтус.

1000 мм · печать 1:1

Изм.	Кол.уч	Лист	№ док.	Подп.	Дата
Разраб.		Кырлан А.С.			21.10.26
Пров.					
ГИП		Кырлан А.С.			21.10.26
Н. контр.					
Утв.					

ГД-2026-004-АИ

Четырёхкомнатная квартира

Общая площадь 102,67* м² · * размеры со скана, не замерены (реестр — л. 6–11, ИЗ-8, К-20, К-21)

Дизайн-проект интерьера четырёхкомнатной квартиры

Стадия	Лист	Листов
РП	82	124

Кухня (пом. 6). Монтажная схема

М 1:20

Кырлан Александр Сергеевич

выпуск 05.10.2026 № 7e7a2cd217 · стр. 92 из 168

Кухня (пом. 6). Развёртка гарнитура

Кухня (пом. 6) · стена В · вид из помещения · размеры в мм, отметки в м

Вид с фасадами

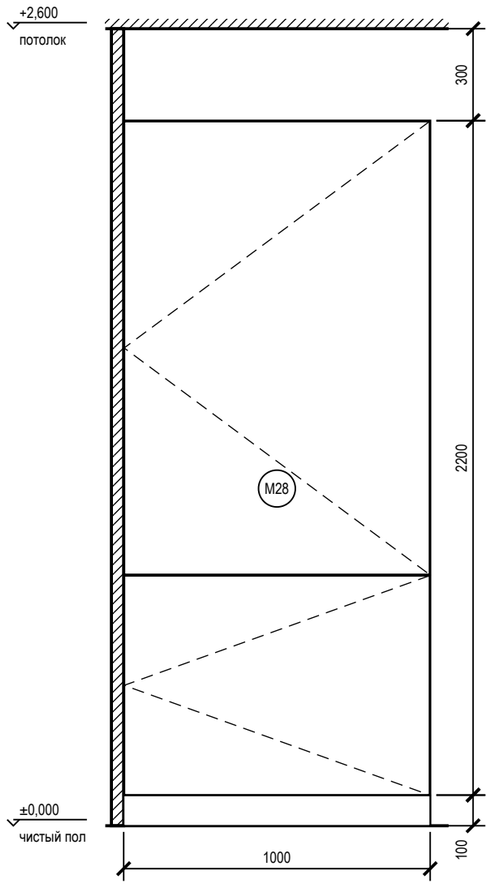

Вид без фасадов (наполнение, выводы)

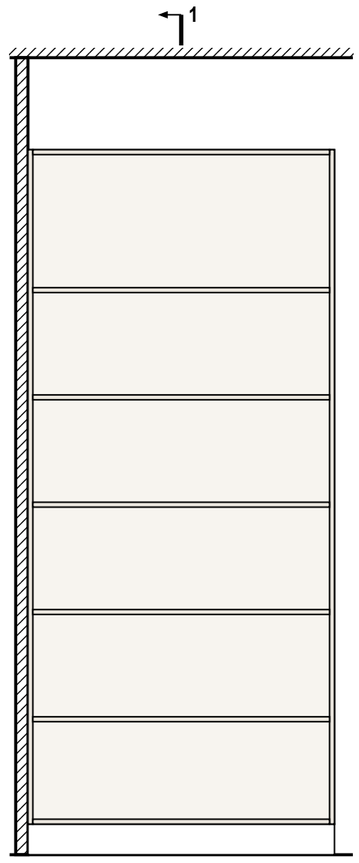

Разрез 1-1

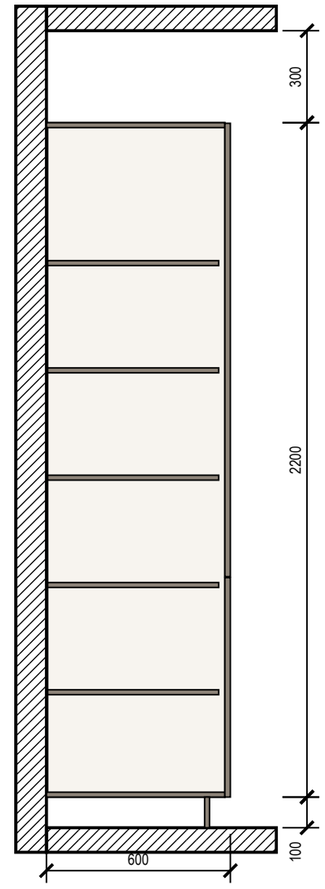

Условные обозначения

- фасад распашной: линии сходятся к стороне петель
- фасад ящика, карго
- встраиваемая техника
- столешница
- доборная планка
- деталь в разрезе
- К1 — марка модуля
- розетка на стене
- вывод кабеля к технике
- В1 — вывод воды В1 / Т3, канализации К1

Примечания

1. Размеры — в мм по чистовой отделке, вид из помещения; марки — как на плане расстановки. Перед раскроем — контрольный замер цеха после фартука и пола.
2. Корпуса — ЛДСП 16 мм, задняя стенка ХДФ 4 мм; фасады — МДФ, эмаль матовая 18 мм, цвет по колерной карте; столешница 38 мм, свес 20 мм; цоколь 100 мм.
3. Кромка: скрытые торцы 0,4 мм, видимые 2 мм. Номинальные зазоры: между фасадами 3 мм, фасад — столешница 3 мм, фасад — стена не менее 3 мм.
4. Ящики полного выдвижения и петли — с доводчиком; присадка по 32-й системе — выполняет цех.
5. Ниши техники — по монтажным схемам выбранных моделей: решётка в цоколе и канал за пеналом холодильника, зазор за духовым шкафом, фасад ПММ на двери машины.

Допущения и предложения на листе

Основа листа: размеры сняты с размерных цепочек растрового скана плана заказчика, на объекте не замерены; ступени наружного контура приведены к граням помещений модели (ИЗ-8, К-20, К-21); высота потолка 2700 мм принята, источника нет (К-24); тип дома и перекрытие (монолит, плита 220 мм) приняты, источника нет (К-3); толщины стен приняты (250 и 120 мм), источника нет (К-21); мощность 15 кВт принята, технических условий нет (К-25).

См. лист открытых вопросов (лист 6, запись К-3; лист 7, записи К-20, К-21, К-24, К-25; лист 10, запись ИЗ-8).

1000 мм · печать 1:1

Изм.	Кол.уч	Лист	№ док.	Подп.	Дата
Разраб.		Кырлан А.С.			21.10.26
Пров.					
ГИП		Кырлан А.С.			21.10.26
Н. контр.					
Утв.					

ГД-2026-004-АИ

Четырёхкомнатная квартира

Общая площадь 102,67* м² · * размеры со скана, не замерены (реестр — л. 6–11, ИЗ-8, К-20, К-21)

Дизайн-проект интерьера четырёхкомнатной квартиры

Стадия	Лист	Листов
РП	83	124

Кухня (пом. 6). Развёртка гарнитура

М 1:20

Кырлан Александр Сергеевич

Кухня (пом. 6). Монтажная схема

Кухня (пом. 6) · стена В · размеры в мм от чистых поверхностей, высоты — от чистого пола

Привязка выводов и крепление модулей

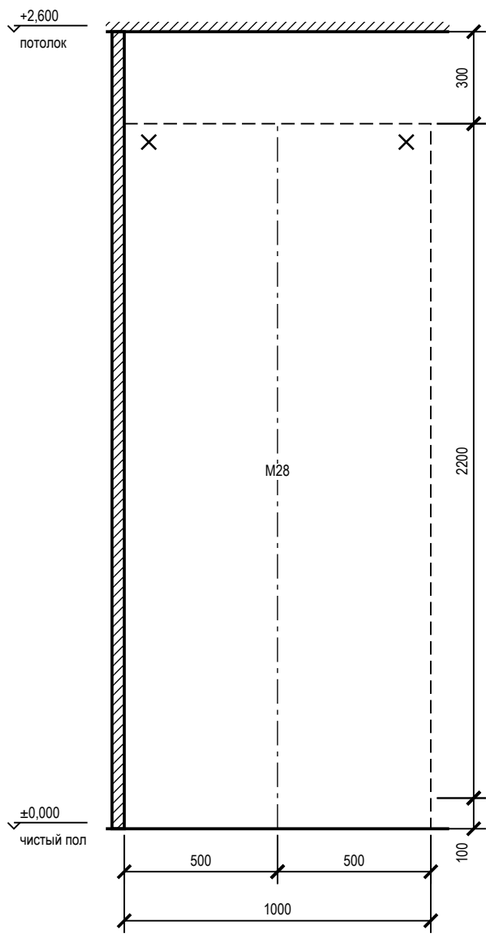

Привязка выводов к осям модулей

Код	Назначение	Модуль	От оси, мм	Н, мм	Размещение

Зазоры под отделку

Поверхность	Отделка	Зазор, мм	Учесть
фартук	керамогранит	10	от чернового основания до корпуса навесных и столешницы
стены	окраска	5	под штукатурку и шпаклёвку за пеналом
пол	инженерная доска		цоколь — после укладки пола, опоры ±20 мм

Условные обозначения

- навесной модуль (невидимый контур)
- ось модуля (от неё — привязка вывода)
- анкер / уголок крепления к стене
- розетка на стене
- вывод кабеля к технике
- B1 — вывод воды В1 / Т3, канализации К1

Примечания

1. Выводы — по проекту электрики и ВК; привязка по горизонтали — от оси модуля (плюс — вправо по виду), по высоте — от чистого пола до оси вывода.
2. Пенал — уголки к стене 2 шт. сверху; нижние модули — стяжками между собой и уголком к стене; ряд выставить по уровню опорами цоколя.
3. Розетки над столешницей — не ниже 150 мм над ней и не за корпусом техники; розетка за ПММ, духовым шкафом и холодильником — только в соседнем модуле или в зоне цоколя с доступом.
4. Столешница — вырезы по шаблонам выбранных моделей мойки и варочной панели; торцы у стены — герметик, пристеночный плинтус.

Допущения и предложения на листе

Основа листа: размеры сняты с размерных цепочек растрового скана плана заказчика, на объекте не замерены; ступени наружного контура приведены к граням помещений модели (ИЗ-8, К-20, К-21); высота потолка 2700 мм принята, источника нет (К-24); тип дома и перекрытие (монолит, плита 220 мм) приняты, источника нет (К-3); толщины стен приняты (250 и 120 мм), источника нет (К-21); мощность 15 кВт принята, технических условий нет (К-25).

Открытые вопросы и конфликты по листу: К-14.

См. лист открытых вопросов (лист 6, запись К-3; лист 7, записи К-14, К-20, К-21, К-24, К-25; лист 10, запись ИЗ-8).

1000 мм · печать 1:1

Изм.	Кол.уч	Лист	№ док.	Подп.	Дата
Разраб.		Кырлан А.С.			21.10.26
Пров.					
ГИП		Кырлан А.С.			21.10.26
Н. контр.					
Утв.					

ГД-2026-004-АИ

Четырёхкомнатная квартира

Общая площадь 102,67* м² · * размеры со скана, не замерены (реестр — л. 6–11, ИЗ-8, К-20, К-21)

Дизайн-проект интерьера четырёхкомнатной квартиры

Стадия	Лист	Листов
РП	84	124

Кухня (пом. 6). Монтажная схема

М 1:20

Кырлан Александр Сергеевич

выпуск 05.10.2026 № 7e7a2cd217 · стр. 94 из 168

Шкафы. Монтажная схема. Лист 1 из 3

крепление к стене, установочные размеры, зазоры под отделку · размеры в мм

Система хранения М8 пом. 2

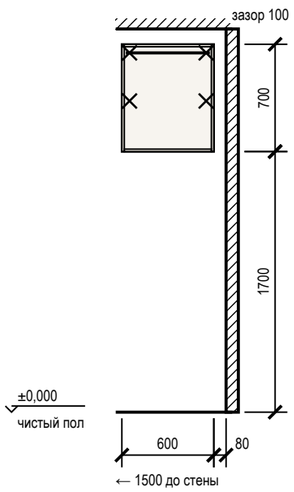

Система хранения М9 (пом. 3)

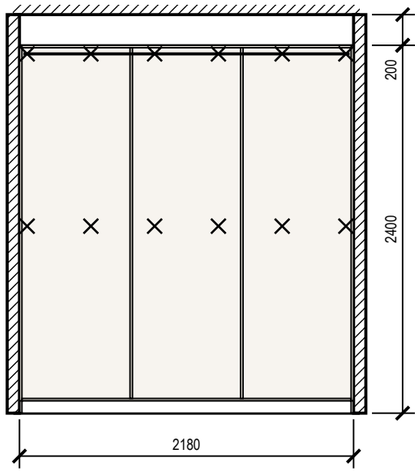

Система хранения М10 (пом. 3)

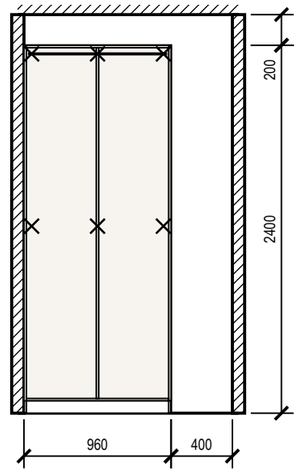

Шкаф распашной М16 (пом. 4)

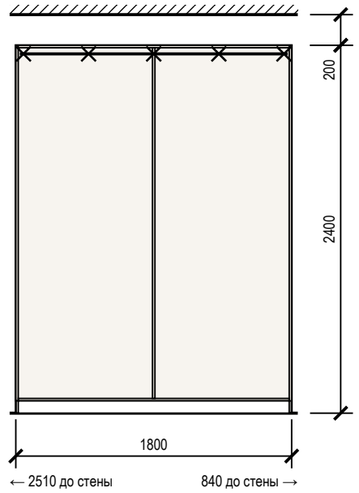

Система хранения М18 (пом. 4)

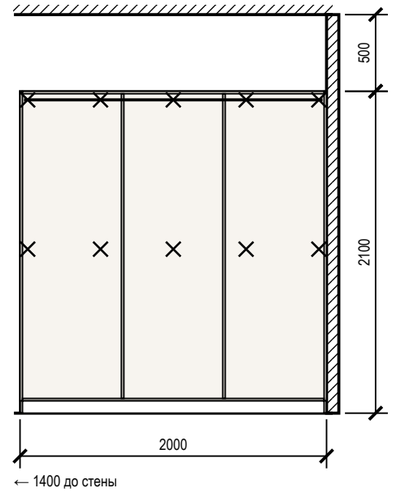

Крепление и зазоры под отделку (изделия листа 1)

Марка	Помещение, стена	Основание	Отделка стены	Зазор, мм	Крепёж по планке	От опрокидывания
М8	Ванная комната (2), стена Б	по основанию — см. таблицу крепежа	плитка	10	анкер 4 шт. (2 ряда)	крепление к стене, 2 точки
М9	Тёмная комната (3), стена Б	по основанию — см. таблицу крепежа	окраска	5	анкер 12 шт. (2 ряда)	крепление к стене, 4 точки
М10	Тёмная комната (3), стена А	по основанию — см. таблицу крепежа	окраска	5	анкер 6 шт. (2 ряда)	крепление к стене, 3 точки
М16	Детская 1 (4), стена В	по основанию — см. таблицу крепежа	окраска	5	анкер 5 шт., шаг 425	уголок к стене, 3 шт.
М18	Детская 1 (4), стена Г	по основанию — см. таблицу крепежа	окраска	5	анкер 10 шт. (2 ряда)	крепление к стене, 3 точки

Крепёж по основанию стены

Основание стены	Крепёж
бетон, ж/б	анкер-шуруп 7,5×72 или дюбель 8×60 с шурупом 5×70
кирпич полнотелый	дюбель 8×80 с шурупом 5×90
газобетон, пазогребень	дюбель для газобетона 10×100 или химический анкер
гипсокартон	закладная до обшивки (брус 40×80 или фанера 18 мм), саморез в закладную

Условные обозначения

- анкер / уголок крепления к стене
- корпус и полки ЛДСП (вид на стену)
- компенсатор — короб до потолка

Примечания

1. Установочные размеры — от чистого пола и чистых стен; перед установкой контрольный замер после отделки.
2. Порядок: корпус выставить по уровню опорами цоколя → закрепить к стене по задней планке → навесить двери и фасады, отрегулировать зазоры → подогнать и закрепить компенсатор.
3. Анкеры — с шагом не более 500 мм, не ближе 50 мм от края планки; на ГКЛ только в закладную, установленную до обшивки.
4. Скрытые коммуникации под анкеры проверить детектором; трассы электрики по плану розеток.
5. Монтажная схема на 3 листах, лист 1 из 3; продолжение — на следующем листе схемы. Условные обозначения, таблица крепежа по основанию и примечания повторены на каждом листе.

Допущения и предложения на листе

Основа листа: размеры сняты с размерных цепочек растрового скана плана заказчика, на объекте не замерены; ступени наружного контура приведены к граням помещений модели (ИЗ-8, К-20, К-21); высота потолка 2700 мм принята, источника нет (К-24); тип дома и перекрытие (монолит, плита 220 мм) приняты, источника нет (К-3); толщины стен приняты (250 и 120 мм), источника нет (К-21); мощность 15 кВт принята, технических условий нет (К-25).

Открытые вопросы и конфликты по листу: К-14.

См. лист открытых вопросов (лист 6, запись К-3; лист 7, записи К-14, К-20, К-21, К-24, К-25; лист 10, запись ИЗ-8).

1000 мм · печать 1:1

Изм.	Кол.уч	Лист	№ док.	Подп.	Дата
Разраб.		Кырлан А.С.			21.10.26
Пров.					
ГИП		Кырлан А.С.			21.10.26
Н. контр.					
Утв.					

ГД-2026-004-АИ

Четырёхкомнатная квартира

Общая площадь 102,67* м² · * размеры со скана, не замерены (реестр — л. 6–11, ИЗ-8, К-20, К-21)

Дизайн-проект интерьера четырёхкомнатной квартиры

Стадия	Лист	Листов
РП	85	124

Шкафы. Монтажная схема. Лист 1 из 3

М 1:40

Кырлан Александр Сергеевич

выпуск 05.10.2026 № 7e7a2cd217 · стр. 95 из 168

Шкафы. Монтажная схема. Лист 2 из 3

ПРЕДВАРИТЕЛЬНО · не для производства работ · открыто пунктов: 30 (реестр — л. 6–11)

крепление к стене, установочные размеры, зазоры под отделку · размеры в мм

Система хранения М19 (пом. 5)

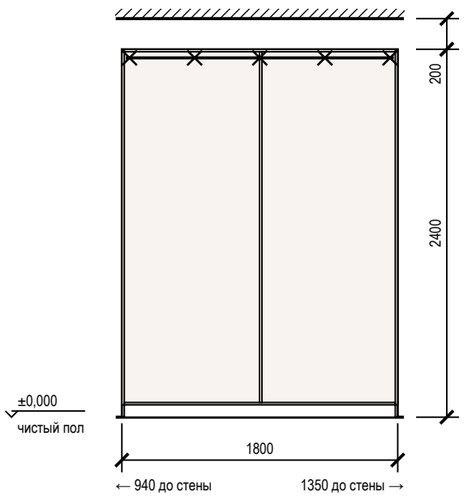

Шкаф-купе М29 (пом. 7)

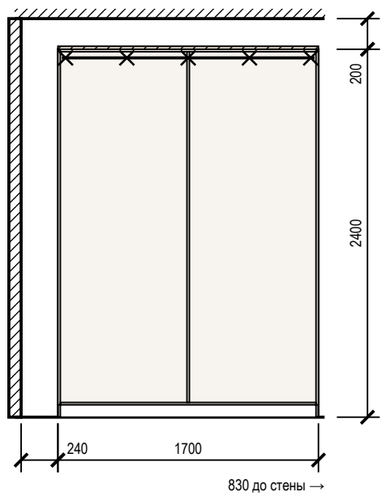

Система хранения М32 пом. 8

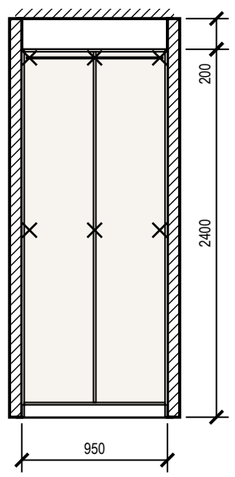

Система хранения М33 (пом. 8)

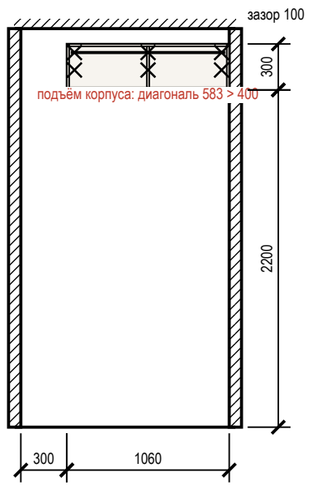

Шкаф распашной М35 (пом. 9)

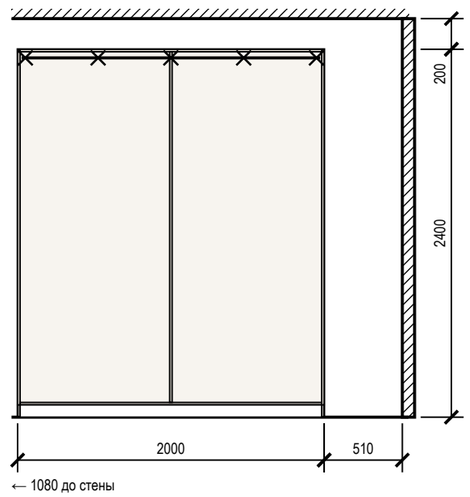

Крепление и зазоры под отделку (изделия листа 2)

Марка	Помещение, стена	Основание	Отделка стены	Зазор, мм	Крепёж по планке	От опрокидывания
М19	Коридор (5), стена А	по основанию — см. таблицу крепежа	окраска	5	анкер 5 шт., шаг 425	крепление к стене, 4 точки
М29	Прихожая-коридор (7), стена Б	по основанию — см. таблицу крепежа	окраска	5	анкер 5 шт., шаг 400	крепление к стене, 3 точки
М32	Гардеробная 2 (8), стена Б	по основанию — см. таблицу крепежа	окраска	5	анкер 6 шт. (2 ряда)	крепление к стене, 3 точки
М33	Гардеробная 2 (8), стена В	по основанию — см. таблицу крепежа	окраска	5	анкер 6 шт. (2 ряда)	крепление к стене, 4 точки
М35	Детская 2 (9), стена А	по основанию — см. таблицу крепежа	окраска	5	анкер 5 шт., шаг 475	уголок к стене, 3 шт.

Крепёж по основанию стены

Основание стены	Крепёж
бетон, ж/б	анкер-шуруп 7,5×72 или дюбель 8×60 с шурупом 5×70
кирпич полнотелый	дюбель 8×80 с шурупом 5×90
газобетон, пазогребень	дюбель для газобетона 10×100 или химический анкер
гипсокартон	закладная до обшивки (брус 40×80 или фанера 18 мм), саморез в закладную

Условные обозначения

- анкер / уголок крепления к стене
- корпус и полки ЛДСП (вид на стену)
- компенсатор — короб до потолка

Примечания

1. Установочные размеры — от чистого пола и чистых стен; перед установкой контрольный замер после отделки.
2. Порядок: корпус выставить по уровню опорами цоколя → закрепить к стене по задней планке → навесить двери и фасады, отрегулировать зазоры → подогнать и закрепить компенсатор.
3. Анкеры — с шагом не более 500 мм, не ближе 50 мм от края планки; на ГКЛ только в закладную, установленную до обшивки.
4. Скрытые коммуникации под анкеры проверить детектором; трассы электрики по плану розеток.
5. Монтажная схема на 3 листах, лист 2 из 3; продолжение — на следующем листе схемы. Условные обозначения, таблица крепежа по основанию и примечания повторены на каждом листе.

Допущения и предложения на листе

Основа листа: размеры сняты с размерных цепочек растрового скана плана заказчика, на объекте не замерены; ступени наружного контура приведены к граням помещений модели (ИЗ-8, К-20, К-21); высота потолка 2700 мм принята, источника нет (К-24); тип дома и перекрытие (монолит, плита 220 мм) приняты, источника нет (К-3); толщины стен приняты (250 и 120 мм), источника нет (К-21); мощность 15 кВт принята, технических условий нет (К-25).

Открытые вопросы и конфликты по листу: К-14.

См. лист открытых вопросов (лист 6, запись К-3; лист 7, записи К-14, К-20, К-21, К-24, К-25; лист 10, запись ИЗ-8).

1000 мм · печать 1:1

Изм.	Кол.уч	Лист	№ док.	Подп.	Дата
Разраб.		Кырлан А.С.			21.10.26
Пров.					
ГИП		Кырлан А.С.			21.10.26
Н. контр.					
Утв.					

ГД-2026-004-АИ

Четырёхкомнатная квартира

Общая площадь 102,67* м² · * размеры со скана, не замерены (реестр — л. 6–11, ИЗ-8, К-20, К-21)

Дизайн-проект интерьера четырёхкомнатной квартиры

Стадия	Лист	Листов
РП	86	124

Шкафы. Монтажная схема. Лист 2 из 3

М 1:40

Кырлан Александр Сергеевич

выпуск 05.10.2026 № 7e7a2cd217 · стр. 96 из 168

Шкафы. Монтажная схема. Лист 3 из 3

крепление к стене, установочные размеры, зазоры под отделку · размеры в мм

Система хранения М39 (пом. 12)

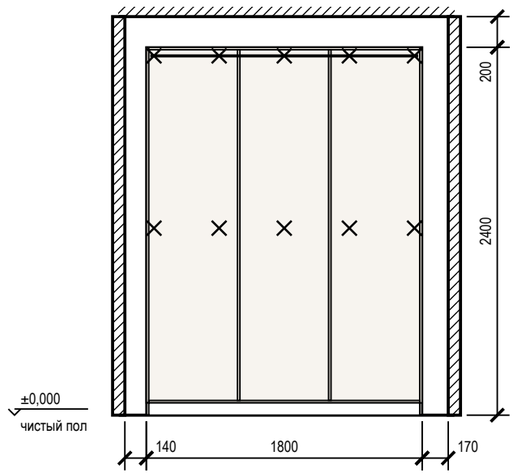

Система хранения М41 пом. 13

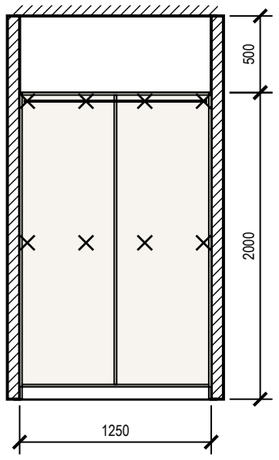

Система хранения М42 пом. 13

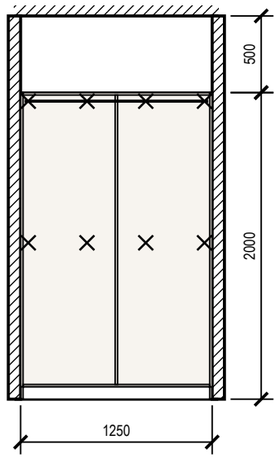

Крепление и зазоры под отделку (изделия листа 3)

Марка	Помещение, стена	Основание	Отделка стены	Зазор, мм	Крепёж по планке	От опрокидывания
М39	Гардеробная 1 (12), стена Б	по основанию — см. таблицу крепежа	окраска	5	анкер 10 шт. (2 ряда)	крепление к стене, 4 точки
М41	Балкон 1 (13), стена Б	по основанию — см. таблицу крепежа	окраска	5	анкер 8 шт. (2 ряда)	крепление к стене, 3 точки
М42	Балкон 1 (13), стена Г	по основанию — см. таблицу крепежа	окраска	5	анкер 8 шт. (2 ряда)	крепление к стене, 3 точки

Крепёж по основанию стены

Основание стены	Крепёж
бетон, ж/б	анкер-шуруп 7,5×72 или дюбель 8×60 с шурупом 5×70
кирпич полнотелый	дюбель 8×80 с шурупом 5×90
газобетон, пазогребень	дюбель для газобетона 10×100 или химический анкер
гипсокартон	закладная до обшивки (брус 40×80 или фанера 18 мм), саморез в закладную

Условные обозначения

- анкер / уголок крепления к стене
- корпус и полки ЛДСП (вид на стену)
- компенсатор — короб до потолка

Примечания

1. Установочные размеры — от чистого пола и чистых стен; перед установкой контрольный замер после отделки.
2. Порядок: корпус выставить по уровню опорами цоколя → закрепить к стене по задней планке → навесить двери и фасады, отрегулировать зазоры → подогнать и закрепить компенсатор.
3. Анкеры — с шагом не более 500 мм, не ближе 50 мм от края планки; на ГКЛ только в закладную, установленную до обшивки.
4. Скрытые коммуникации под анкеры проверить детектором; трассы электрики по плану розеток.
5. Монтажная схема на 3 листах, лист 3 из 3. Условные обозначения, таблица крепежа по основанию и примечания повторены на каждом листе.

Допущения и предложения на листе

Основа листа: размеры сняты с размерных цепочек растрового скана плана заказчика, на объекте не замерены; ступени наружного контура приведены к граням помещений модели (ИЗ-8, К-20, К-21); высота потолка 2700 мм принята, источника нет (К-24); тип дома и перекрытие (монолит, плита 220 мм) приняты, источника нет (К-3); толщины стен приняты (250 и 120 мм), источника нет (К-21); мощность 15 кВт принята, технических условий нет (К-25).

Открытые вопросы и конфликты по листу: К-14.

См. лист открытых вопросов (лист 6, запись К-3; лист 7, записи К-14, К-20, К-21, К-24, К-25; лист 10, запись ИЗ-8).

1000 мм · печать 1:1

Изм.	Кол.уч	Лист	№ док.	Подп.	Дата
Разраб.		Кырлан А.С.			21.10.26
Пров.					
ГИП		Кырлан А.С.			21.10.26
Н. контр.					
Утв.					

ГД-2026-004-АИ

Четырёхкомнатная квартира

Общая площадь 102,67* м² · * размеры со скана, не замерены (реестр — л. 6–11, ИЗ-8, К-20, К-21)

Дизайн-проект интерьера четырёхкомнатной квартиры

Стадия	Лист	Листов
РП	87	124

Шкафы. Монтажная схема. Лист 3 из 3

М 1:40

Кырлан Александр Сергеевич

выпуск 05.10.2026 № 7e7a2cd217 · стр. 97 из 168

Ведомости изделий, техники и фурнитуры

встроенная мебель и кухонный гарнитур · размеры в мм

Ведомость изделий

Марка	Наименование	Пом.	Ш×Г×В, мм	Корпус	Фасад	Кромка, мм скр./вид.	Кол.
М8	Система хранения	2	600×350×700	ЛДСП 16	без фасадов; ящики — МДФ 18, эмаль матовая	0,4 / 2	1
М9	Система хранения	3	2180×400×2400	ЛДСП 16	без фасадов; ящики — МДФ 18, эмаль матовая	0,4 / 2	1
М10	Система хранения	3	960×400×2400	ЛДСП 16	без фасадов; ящики — МДФ 18, эмаль матовая	0,4 / 2	1
М16	Шкаф распашной	4	1800×600×2400	ЛДСП 16	МДФ 18, эмаль матовая	0,4 / 2	1
М18	Система хранения	4	2000×350×2100	ЛДСП 16	без фасадов; ящики — МДФ 18, эмаль матовая	0,4 / 2	1
М19	Система хранения	5	1800×250×2400	ЛДСП 16	МДФ 18, эмаль матовая	0,4 / 2	1
М29	Шкаф-купе	7	1700×600×2400	ЛДСП 16	рифлёные панели МДФ в алюминиевом профиле	0,4 / 2	1
М32	Система хранения	8	950×300×2400	ЛДСП 16	без фасадов; ящики — МДФ 18, эмаль матовая	0,4 / 2	1
М33	Система хранения	8	1060×500×300	ЛДСП 16	без фасадов; ящики — МДФ 18, эмаль матовая	0,4 / 2	1
М35	Шкаф распашной	9	2000×600×2400	ЛДСП 16	МДФ 18, эмаль матовая	0,4 / 2	1
М39	Система хранения	12	1800×600×2400	ЛДСП 16	без фасадов; ящики — МДФ 18, эмаль матовая	0,4 / 2	1
М41	Система хранения	13	1250×400×2000	ЛДСП 16	без фасадов; ящики — МДФ 18, эмаль матовая	0,4 / 2	1
М42	Система хранения	13	1250×380×2000	ЛДСП 16	без фасадов; ящики — МДФ 18, эмаль матовая	0,4 / 2	1
М20	Пенал: холодильник встр.	6	600×600×2300	ЛДСП 16	МДФ 18, эмаль матовая	0,4 / 2	1
М21	Модуль нижний: ящики	6	600×600×900	ЛДСП 16	МДФ 18, эмаль матовая	0,4 / 2	1
М24	Модуль навесной: полки	6	600×350×720	ЛДСП 16	МДФ 18, эмаль матовая	0,4 / 2	1
М22	Модуль нижний: духовой шкаф, варочная	6	600×600×900	ЛДСП 16	МДФ 18, эмаль матовая	0,4 / 2	1
М25	Модуль навесной: полки	6	600×350×600	ЛДСП 16	МДФ 18, эмаль матовая	0,4 / 2	1
М23	Модуль нижний: ящики	6	600×600×900	ЛДСП 16	МДФ 18, эмаль матовая	0,4 / 2	1
М26	Модуль навесной: полки	6	600×350×720	ЛДСП 16	МДФ 18, эмаль матовая	0,4 / 2	1
М28	Пенал: полки	6	1000×600×2300	ЛДСП 16	МДФ 18, эмаль матовая	0,4 / 2	1

Ведомость встраиваемой техники

Поз.	Прибор	Ниша, вырез, мм	Вентиляция	Питание	Схема
М20	Холодильник встраиваемый, ниша 1780	ниша 1780 × 560 × 550	решётка в цоколе, канал за корпусом, выход сверху	розетка над нишей или в соседнем модуле	по модели
М22	Духовой шкаф встраиваемый, 60 см	ниша 560 × 595, глубина ≥ 550	зазор за шкафом, вырез в задней стенке	вывод кабеля под шкафом	по модели
М22	Варочная панель индукционная, 60 см	вырез в столешнице 560 × 490		вывод кабеля под модулем	по модели
М22	Вытяжка настенная, 60 см	низ ≥ 650 над панелью	воздуховод к вентканалу, короб до потолка	вывод кабеля в коробе	по модели

Ведомость фурнитуры

№	Фурнитура	Тип, размер	Изделия	Кол.
1	Полкодержатель с фиксацией	ø5 мм	М8, М9, М10, М16, М18, М19, М29, М32, М33, М35, М39, М41, М42, М20, М24, М25, М26, М28	344
2	Штанга выдвижная торцевая	L по глубине	М8, М9, М10, М18, М33, М41, М42	11
3	Анкер по основанию стены	по таблице крепежа	М8, М9, М10, М16, М18, М19, М29, М32, М33, М35, М39, М41, М42, М24, М25, М26	96
4	Уголок крепления к стене от опрокидывания	стальной	М8, М9, М10, М16, М18, М19, М29, М32, М33, М35, М39, М41, М42, М20, М28	30
5	Опора регулируемая с цоколем на клипсах	ход 20 мм	М9, М10, М16, М18, М19, М29, М32, М35, М39, М41, М42	80
6	Петля накладная 110° с доводчиком	чашка 35 мм	М16, М19, М35, М20, М24, М25, М26, М28	96
7	Штанга овальная 30×15, L = 876	+ 2 держателя	М16	1
8	Система дверей купе: профиль, направляющие, ролики	на 2 двери	М29	1
9	Ручка-профиль вертикальная	в цвет профиля	М29	2
10	Штанга овальная 30×15, L = 826	+ 2 держателя	М29	1
11	Полка для обуви выдвижная наклонная	ширина 826	М29	3
12	Штанга овальная 30×15, L = 976	+ 2 держателя	М35	1
13	Штанга овальная 30×15, L = 579	+ 2 держателя	М39	3
14	Ручка-профиль	латунь матовая	М20, М21, М24, М22, М25, М23, М26, М28	18
15	Опора кухонная регулируемая 100–120 мм	+ клипса цоколя	М20, М21, М22, М23, М28	22
16	Направляющие полного выдвижения с доводчиком NL 500	пара	М21, М22, М23	7
17	Навес регулируемый для навесного шкафа	пара на секцию	М24, М25, М26	3
18	Шина монтажная	L = 540	М24, М25, М26	3

Примечания

1. Модели техники выбирает заказчик до изготовления мебели; ниши, вырезы и вентиляция — по монтажной схеме выбранной модели (условие гарантии), её номер вносится в ведомость.
2. Количество фурнитуры — по чертежам изделий; запас крепежа 5 %. Аналоги — по характеристикам (доводчик, нагрузка, ход).
3. Цвет корпусов, фасадов и профилей — по колерной карте проекта.

Допущения и предложения на листе

Основа листа: размеры сняты с размерных цепочек растрового скана плана заказчика, на объекте не замерены; ступени наружного контура приведены к граням помещений модели (ИЗ-8, К-20, К-21); высота потолка 2700 мм принята, источника нет (К-24); тип дома и перекрытие (монолит, плита 220 мм) приняты, источника нет (К-3); толщины стен приняты (250 и 120 мм), источника нет (К-21); мощность 15 кВт принята, технических условий нет (К-25).

См. лист открытых вопросов (лист 6, запись К-3; лист 7, записи К-20, К-21, К-24, К-25; лист 10, запись ИЗ-8).

Изм.	Кол.уч	Лист	№ док.	Подп.	Дата
Разраб.		Кырлан А.С.			21.10.26
Пров.					
ГИП		Кырлан А.С.			21.10.26
Н. контр.					
Утв.					

ГД-2026-004-АИ

Четырёхкомнатная квартира

Общая площадь 102,67* м² · * размеры со скана, не замерены (реестр — л. 6–11, ИЗ-8, К-20, К-21)

Дизайн-проект интерьера четырёхкомнатной квартиры

Стадия	Лист	Листов
РП	88	124

Ведомости изделий, техники и фурнитуры

М б/м

Кырлан Александр Сергеевич

выпуск 05.10.2026 № 7e7a2cd217 · стр. 98 из 168

09

Развёртки и узлы

Кырлан Александр Сергеевич

выпуск 05.10.2026 · 7e7a2cd217 · стр. 99 из 168

Реестр марок отделки и позиций альбома

Реестр марок отделки (О ↔ позиции колерной карты) и марки позиций по видам

Реестр марок отделки альбома

Марка	Поверхность	Материал, изделие	Цвет, код	Помещения	Колер. карта
О1	стены	окраска, Tikkurila Optiva 5 Matt, матовая, подготовка К3	Tikkurila F497 «Paper»	1, 3, 8, 11, 12	К1
О2	акцентная стена	окраска, Tikkurila Optiva 5 Matt, аналог: интерьерная краска, класс 2 по EN 13300, глубокоматовая/матовая, база С, матовая, подготовка К3	Tikkurila L481 «Silhouette»	1, 11	К2
О3	плинтус	плинтус МДФ, h 80 мм, аналог: плинтус МДФ под окраску 80×16 мм, полуглянцевая	Tikkurila F497 «Paper»	1, 3, 4, 6, 8, 9, 11, 12	К4
О4	потолок	окраска, Tikkurila Anti-Reflex 2, глубокоматовая, подготовка Q3	Tikkurila F497 «Paper»	1, 3, 4, 5, 7, 8, 9, 11, 12	К3
О5	пол	инженерная доска, аналог: дуб натуральный брашированный, масло-воск, 14/4 мм		1, 3, 4, 6, 8, 9, 11, 12	КМ1
О6	стены	облицовка плиткой, 600×600×9 мм, аналог: керамогранит матовый, тон F497, затирка CG2WA	#F1F1EC «тон Paper F497»	2, 10	КМ2
О7	потолок	окраска, Tikkurila Luja 7, матовая, подготовка Q3	Tikkurila F497 «Paper»	2, 6, 10, 13	К5
О8	пол	керамогранит, 600×600×10 мм, аналог: керамогранит матовый R10, тон J484	#CEBFB0 «тон Castle J484»	2, 10	КМ3
О9	стены	окраска, Tikkurila Joker, шелковисто-матовая, подготовка К3	Tikkurila F497 «Paper»	4, 9	К6
О10	стены	окраска, Tikkurila Optiva 20 Semimatt, шелковисто-матовая, подготовка К3	Tikkurila J484 «Castle»	5, 7	К7
О11	плинтус	плинтус МДФ, h 80 мм, аналог: плинтус МДФ под окраску 80×16 мм, полуглянцевая	Tikkurila J484 «Castle»	5, 7	К8
О12	пол	керамогранит, 600×600×10 мм, аналог: керамогранит матовый R10, тон V486	#B8AFA5 «тон Claystone V486»	5, 7	КМ4
О13	стены	окраска, Tikkurila Luja 7, шелковисто-матовая, подготовка К3	Tikkurila F497 «Paper»	6, 13	К9
О14	фартук	керамогранит, 600×600×9 мм, аналог: керамогранит матовый, тон F497, затирка CG2WA	#F1F1EC «тон Paper F497»	6	КМ5
О15	плинтус	керамогранит, аналог: плинтус из керамогранита пола, подрезка 80 мм, верхняя кромка с запилом 45°	#B8AFA5 «тон Claystone V486»	13	КМ7
О16	пол	керамогранит, аналог: керамогранит матовый R11, тон V486, затирка CG2WA	#B8AFA5 «тон Claystone V486»	13	КМ6

Марки позиций альбома по видам

Префикс	Что обозначает, позиции	Листы
Д	двери: Д-1–Д-5	20–22
ОК	окна: ОК-1–ОК-6	20–22
М	мебель и оборудование: М1–М35, М36*, М37–М39, М41–М43	23–28
П	сантехнические приборы: П1–П9	40–42
ДК	декор (картины, зеркала, растения): ДК1–ДК15, ДК16**, ДК17–ДК19, ДК20**, ДК21**	1, 62–66
Т	текстиль (шторы, ковры): Т1–Т15, Т16**, Т17**, Т18–Т23	1, 62–66

Допущения и предложения на листе. Знак «*» принято (замерить). Знак «**» предложено (согласовать): пол пом. 1–13, плинтус пом. 1, 3–9, 11–13, акцент пом. 1, 11, стены пом. 2, 10, фартук пом. 6. См. лист открытых вопросов (листы 6–11).

Марки позиций альбома по видам (продолжение)

Префикс	Что обозначает, позиции	Листы
Р	розетки: Р1–Р20, Р21**, Р22–Р26, Р27**, Р28–Р32, Р33**, Р34, Р35, Р36**, Р37**, Р38**	29–37
ТВ	розетки ТВ: ТВ1	29–37
LAN	розетки компьютерные: LAN1–LAN3, LAN4**	29–37
S	выключатели: S1, S2**, S3, S4**, S5–S15, S16**, S17**, S18**	29–37
Св	светильники: Св1–Св12, Св13**, Св14–Св19, Св20**, Св21–Св24, Св25**, Св26–Св54, Св56–Св62, Св63**, Св64**, Св65**, Св66**, Св67**	29–37
БП	блоки питания LED: БП1, БП2	29–37
ИП	извещатели: ИП1, ИП2, ИП3**, ИП4, ИП5**, ИП6, ИП7	29–37
ЭВ	выводы кабеля: ЭВ1, ЭВ2**, ЭВ3, ЭВ4, ЭВ5**	29–37
КУП, ТР	электроустановочные изделия: КУП1**, КУП2**, ТР1, ТР2	29–37
ЩК**, ЩС**	щиты: ЩК1**, ЩС**	29–37
АР	точки доступа Wi-Fi: АР1**, АР2**	29–37
Ст В1, Ст К1, Ст Т3	стояки (системы В1, Т3, К1): Ст В1-1, Ст В1-2*, Ст К1-1, Ст К1-2*, Ст Т3-1	40–42
О	марки отделки (реестр альбома): О1–О16	2–5, 89–117
К, КМ	позиции колерной карты: К1–К9, КМ1–КМ7	58–61
РО	радиаторы отопления: РО-1–РО-5	38, 39

Примечания

1. Марка отделки О — одна на весь альбом: одна и та же отделка (материал, изделие, цвет, формат) на всех листах имеет одну марку; на развёртках и планах стоят марки этого реестра.
2. Столбец «Колер. карта» — позиции колерной карты (лист 58): К — окраска по коду цвета, КМ — материал без кода цвета; «Помещения» — номера по экспликации; количества — по ведомости отделки помещений (лист 55).
3. Марки позиций: один префикс — один вид позиций на весь альбом (двери Д, окна ОК, мебель М, сантехприборы П, декор ДК, текстиль Т, колерная карта К и КМ, радиаторы РО, розетки Р, выключатели S, светильники Св; стояки — «Ст» и система, например «Ст К1-1»). Совпадение префиксов у разных видов — замечание к исходным данным, при выпуске исправляется в модели.

Изм.	Кол.уч	Лист	№ док.	Подп.	Дата	ГД-2026-004-АИ		
						Четырёхкомнатная квартира Общая площадь 102,67* м² · * размеры со скана, не замерены (реестр — л. 6–11, ИЗ-8, К-20, К-21)		
Разраб.		Кырлан А.С.			21.10.26	Дизайн-проект интерьера четырёхкомнатной квартиры	Стадия: РП	Лист: 89 / Листов: 124
Пров.								
ГИП		Кырлан А.С.			21.10.26			
Н. контр.						Реестр марок отделки и позиций альбома М б/м	Кырлан Александр Сергеевич	
Утв.								

выпуск 05.10.2026 № 7e7a2cd217 · стр. 100 из 168

Схема расположения развёрток и узлов

План квартиры: марки развёрток по помещениям, выноски узлов, ведомость «марка → лист»

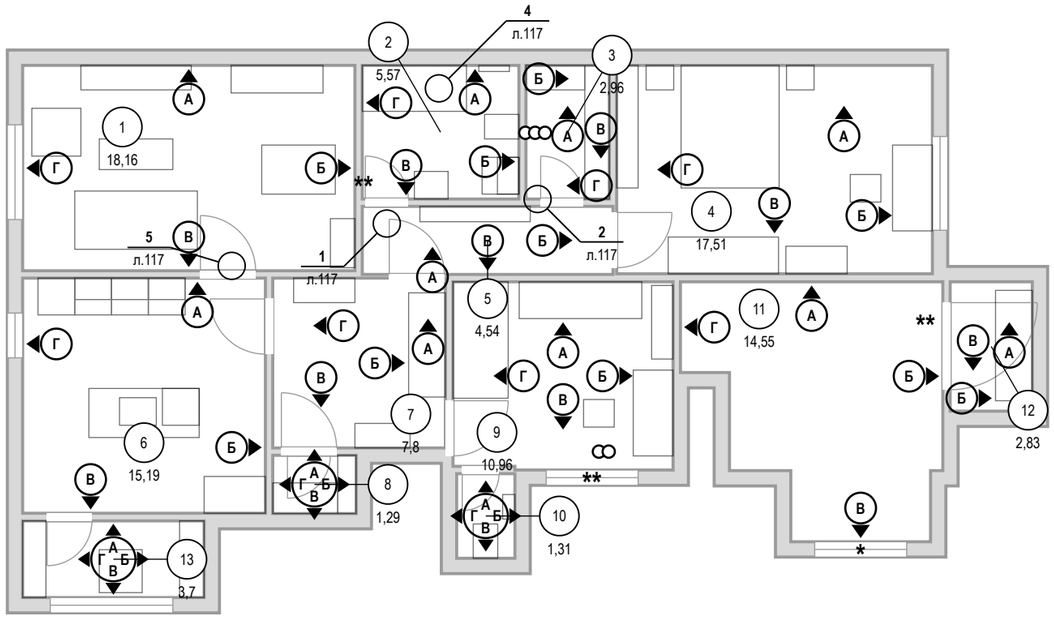

Развёртки и узлы: марка → лист

Марка	Помещение / узел	Лист
А, Б	Зал (пом. 1)	91
В, Г	Зал (пом. 1)	92
А	Ванная комната (пом. 2)	93
Б	Ванная комната (пом. 2)	94
В	Ванная комната (пом. 2)	95
Г	Ванная комната (пом. 2)	96
А, Б, В, Г	Тёмная комната (пом. 3)	97
А, Б	Детская 1 (пом. 4)	98
В, Г	Детская 1 (пом. 4)	99
А, Б	Коридор (пом. 5)	100
В	Коридор (пом. 5)	101
А	Кухня (пом. 6)	102
Б, В	Кухня (пом. 6)	103
Г	Кухня (пом. 6)	104
А, Б, В	Прихожая-коридор (пом. 7)	105
Г	Прихожая-коридор (пом. 7)	106
А, Б, В, Г	Гардеробная 2 (пом. 8)	107
А, Б	Детская 2 (пом. 9)	108
В, Г	Детская 2 (пом. 9)	109
А, Б	Санузел (пом. 10)	110
В, Г	Санузел (пом. 10)	111
А, Б	Гостиная (пом. 11)	112
В, Г	Гостиная (пом. 11)	113
А, Б, В	Гардеробная 1 (пом. 12)	114
А, Б, В	Балкон 1 (пом. 13)	115
Г	Балкон 1 (пом. 13)	116
узел 1	Порог 15 мм: мокрая зона — жилое помещение	117
узел 2	Стык покрытий пола Т-профилем без перепада	117
узел 3	Короб стояков К1-1, В1-1, Т3-1 с люком и звукоизоляцией	117
узел 4	Гидроизоляция санузла: заход на стены 200 мм, примыкание ванны	117
узел 5	Плинтус МДФ 80×16 мм у окрашенной стены	117

Допущения и предложения на листе

Основа листа: размеры сняты с размерных цепочек растрового скана плана заказчика, на объекте не замерены; ступени наружного контура приведены к граням помещений модели (ИЗ-8, К-20, К-21); высота потолка 2700 мм принята, источника нет (К-24); тип дома и перекрытие (монолит, плита 220 мм) приняты, источника нет (К-3); толщины стен приняты (250 и 120 мм), источника нет (К-21); мощность 15 кВт принята, технических условий нет (К-25).

Знак «*» — принято, не замерено и не подтверждено (замерить на объекте): К-1, К-15: Ст К1-2, Ст В1-2; К-22: окно пом. 11 (стена В).

Знак «**» — предложение проектировщика, заказчиком не утверждено (согласовать с заказчиком): ИЗ-1, К-1: окно пом. 9 (стена В); ИЗ-6: дверь пом. 12 (стена Г); ИЗ-8: дверь пом. 2 (стена В) — смещение 100 → 110 мм (откос до угла был 40 мм при норме от 50 мм).

См. лист открытых вопросов (лист 6, записи К-1, К-3; лист 7, записи К-15, К-20–К-22, К-24, К-25; лист 9, записи ИЗ-1, ИЗ-6; лист 10, запись ИЗ-8).

Условные обозначения

- А — марка развёртки: буква стены, стрелка — взгляд
- выноска узла: над полкой — узел, под полкой — лист
- 1 — номер помещения, площадь м²

1000 мм · печать 1:1

Примечания

1. Развёртки — вид на стену изнутри помещения; буквы стен — одна система на весь альбом (как на листах выводов, плитки и отделки).
2. Стены без электроточек, мебели, декора и акцентной отделки развёрток не имеют: их отделка — по ведомости отделки помещений.
3. Узлы — на листе узлов; места применения — по выноскам этого листа и ведомости «марка → лист».

Изм.	Кол.уч	Лист	№ док.	Подп.	Дата
Разраб.		Кырлан А.С.			21.10.26
Пров.					
ГИП		Кырлан А.С.			21.10.26
Н. контр.					
Утв.					

ГД-2026-004-АИ

Четырёхкомнатная квартира

Общая площадь 102,67* м² · * размеры со скана, не замерены (реестр — л. 6–11, ИЗ-8, К-20, К-21)

Дизайн-проект интерьера четырёхкомнатной квартиры

Стадия	Лист	Листов
РП	90	124

Схема расположения развёрток и узлов

М 1:100

Кырлан Александр Сергеевич

выпуск 05.10.2026 № 7e7a2cd217 · стр. 101 из 168

Развёртки стен А, Б. Зал (пом. 1)

Зал (пом. 1) · вид изнутри помещения · размеры в мм, отметки в м

ПРЕДВАРИТЕЛЬНО · не для производства работ · открыто пунктов: 30 (реестр — л. 6–11)

Развёртка стены А

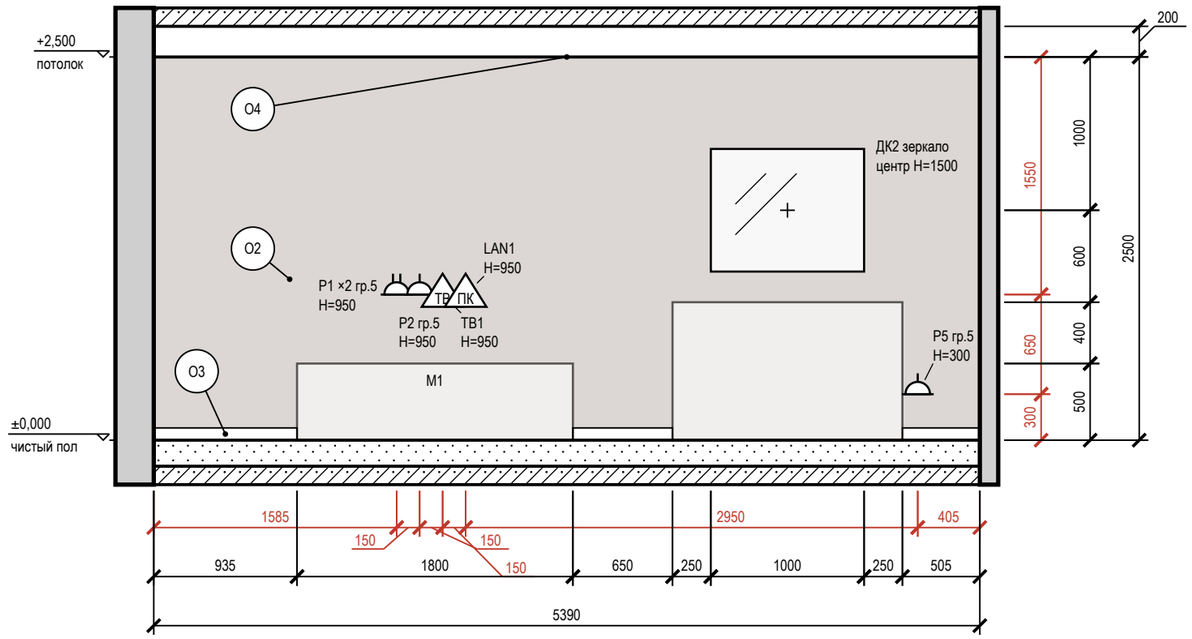

Развёртка стены Б

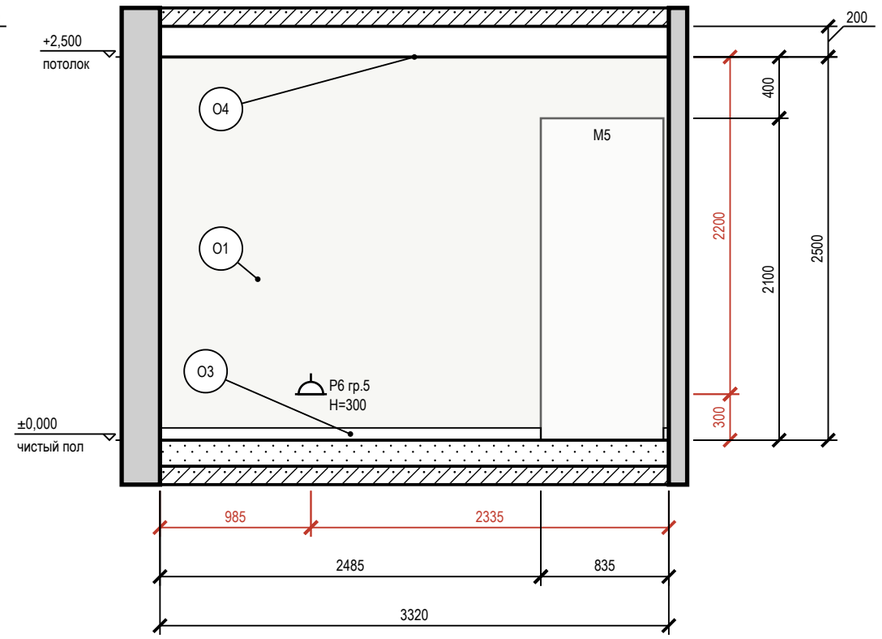

Схема развёрток (М 1:100)

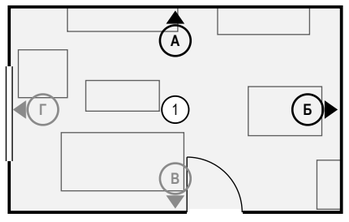

Условные обозначения

- розетка с заземляющим контактом; у знака — марка, ×N постов в рамке, гр. — группа щита, Н — высота оси, мм
- ПК — розетка компьютерная RJ45
- ТВ — розетка телевизионная
- привязки точек и выводов от угла и от пола, мм
- мебель и приборы — фасад по расстановке (условно)
- зеркало: марка Д, крест — центр, Н — высота центра, мм
- стены и перекрытия в сечении
- окраска: тон — цвет по коду производителя (условно)
- О1 — марка отделки по реестру отделки альбома
- А — марка развёртки: буква стены, стрелка — взгляд

Ведомость отделки (на листе)

Марка	Поверхность	Материал, изделие	Цвет, код	Кол.
О1	стены	окраска, Tikkurila Optiva 5 Matt, матовая, подготовка К3	Tikkurila F497 «Paper»	8,3 м²
О2	акцентная стена	окраска, Tikkurila Optiva 5 Matt, аналог: интерьерная краска, класс 2 по EN 13300, глубокоматовая/матовая, база С, матовая, подготовка К3	Tikkurila L481 «Silhouette»	13,5 м²
О3	плинтус	плинтус МДФ, h 80 мм, аналог: плинтус МДФ под окраску 80×16 мм, полуглянцевая	Tikkurila F497 «Paper»	4,6 м
О4	потолок	окраска, Tikkurila Anti-Reflex 2, глубокоматовая, подготовка Q3	Tikkurila F497 «Paper»	18,2 м²

Допущения и предложения на листе

Основа листа: размеры сняты с размерных цепочек растрового скана плана заказчика, на объекте не замерены; ступени наружного контура приведены к граням помещений модели (ИЗ-8, К-20, К-21); высота потолка 2700 мм принята, источника нет (К-24); тип дома и перекрытие (монолит, плита 220 мм) приняты, источника нет (К-3); толщины стен приняты (250 и 120 мм), источника нет (К-21); мощность 15 кВт принята, технических условий нет (К-25).

См. лист открытых вопросов (лист 6, запись К-3; лист 7, записи К-20, К-21, К-24, К-25; лист 10, запись ИЗ-8).

Примечания

1. Развёртки — вид на стену изнутри помещения, по часовой стрелке; расположение — на схеме листа и на листе 90; размеры — в мм по чистовым поверхностям; отметки — в м от ±0,000; высоты Н — от чистого пола помещения до оси изделия, у декора — до центра.
2. Красные цепочки — привязки электроточек и выводов: по горизонтали от угла чистовых стен, по вертикали от чистого пола, до оси изделия; звенья короче 3 мм на листе вынесены во второй ярус (ближняя к стене цепочка).
3. У знака электроточки: марка (Р — розетка, S — выключатель, Св — светильник, ЭВ — вывод кабеля), ×N — число постов в рамке, гр. — группа щита, Н — высота оси от чистого пола, мм; группы по клавишам выключателя — на листе выключателей.
4. Схема мебели, приборов и декора не является технической документацией для производства мебели; габариты — по паспортам изделий.
5. Картины и зеркала крепить к основанию по паспорту изделия (закладные и анкеры — в перечне скрытых работ); крест — ось центра предмета.
6. Потолок на развёртках — по нижнему уровню У1; другие уровни потолка помещения: У2 +2,600.

1000 мм · печать 1:1

Изм.	Кол.уч	Лист	№ док.	Подп.	Дата
Разраб.		Кырлан А.С.			21.10.26
Пров.					
ГИП		Кырлан А.С.			21.10.26
Н. контр.					
Утв.					

ГД-2026-004-АИ

Четырёхкомнатная квартира

Общая площадь 102,67* м² · * размеры со скана, не замерены (реестр — л. 6–11, ИЗ-8, К-20, К-21)

Дизайн-проект интерьера четырёхкомнатной квартиры

Стадия	Лист	Листов
РП	91	124

Развёртки стен А, Б. Зал (пом. 1)

М 1:40

Кырлан Александр Сергеевич

выпуск 05.10.2026 № 7e7a2cd217 · стр. 102 из 168

Развёртки стен В, Г. Зал (пом. 1)

Зал (пом. 1) · вид изнутри помещения · размеры в мм, отметки в м

ПРЕДВАРИТЕЛЬНО · не для производства работ · открыто пунктов: 30 (реестр — л. 6–11)

Развёртка стены В

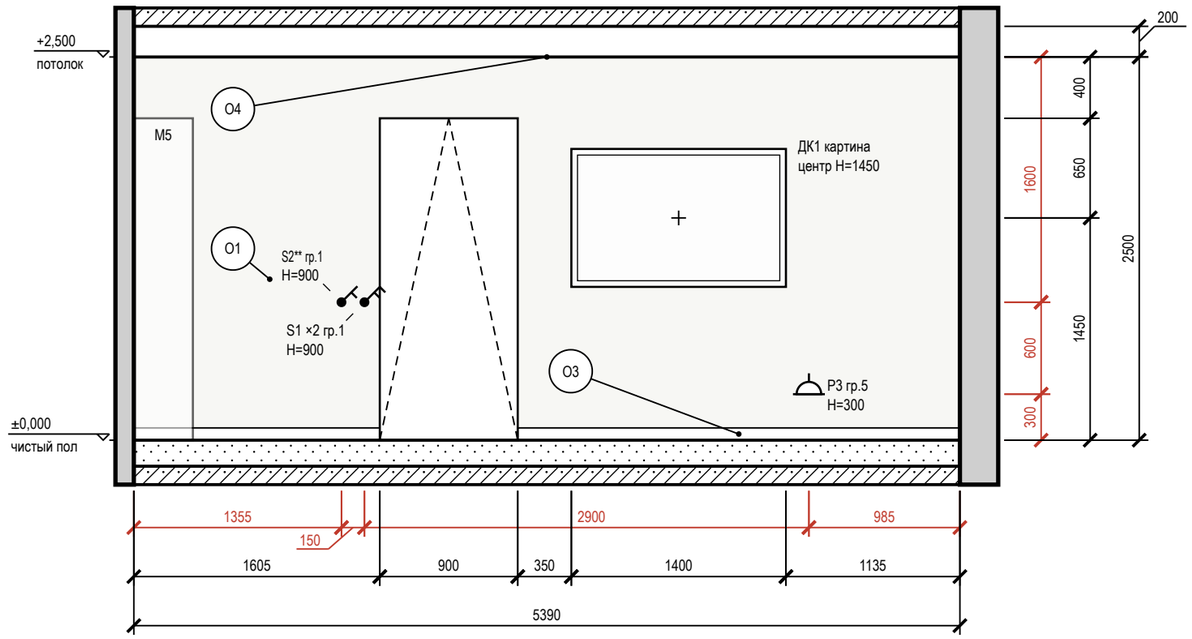

Развёртка стены Г

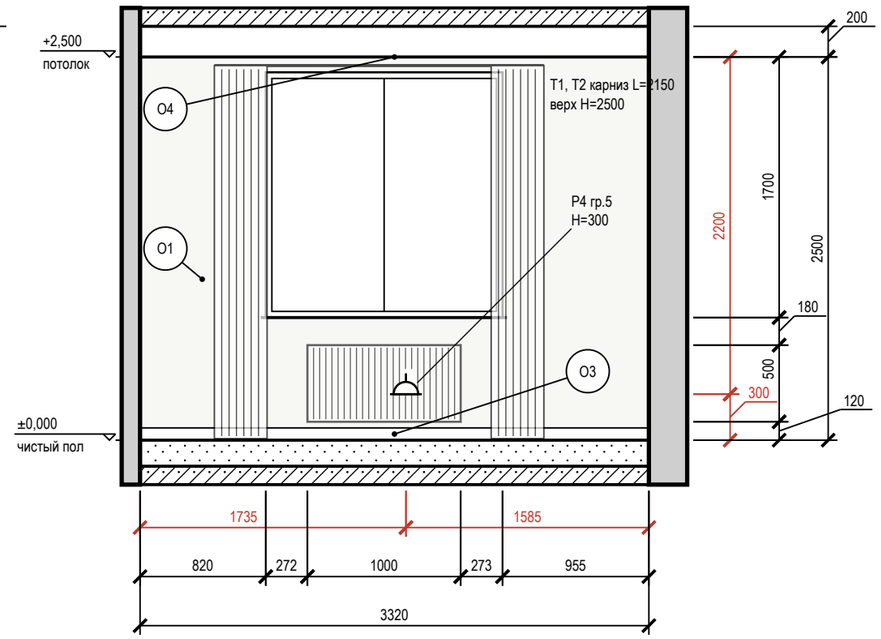

Схема развёрток (М 1:100)

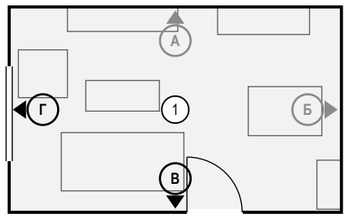

Условные обозначения

- розетка с заземляющим контактом; у знака — марка, ×N постов в рамке, гр. — группа щита, H — высота оси, мм
- выключатель одноклавишный
- выключатель двухклавишный (флажков — по числу клавиш)
- привязки точек и выводов от угла и от пола, мм
- мебель и приборы — фасад по расстановке (условно)
- картина (декор): марка Д, крест — центр, H — высота центра, мм
- карниз (шина) и шторы в собранном виде: марка Т, длина L, верх H
- окно: проём, рама, подоконник
- дверной проём; марка двери — в кружке
- радиатор отопления; марка — по плану отопления
- стены и перекрытия в сечении
- окраска: тон — цвет по коду производителя (условно)
- О1 — марка отделки по реестру отделки альбома
- А — марка развёртки: буква стены, стрелка — взгляд

Ведомость отделки (на листе)

Марка	Поверхность	Материал, изделие	Цвет, код	Кол.
О1	стены	окраска, Tikkurila Optiva 5 Matt, матовая, подготовка К3	Tikkurila F497 «Paper»	17,4 м²
О3	плинтус	плинтус МДФ, h 80 мм, аналог: плинтус МДФ под окраску 80×16 мм, полуглянцевая	Tikkurila F497 «Paper»	7,8 м
О4	потолок	окраска, Tikkurila Anti-Reflex 2, глубокоматовая, подготовка Q3	Tikkurila F497 «Paper»	18,2 м²

Допущения и предложения на листе

Основа листа: размеры сняты с размерных цепочек растрового скана плана заказчика, на объекте не замерены; ступени наружного контура приведены к граням помещений модели (ИЗ-8, К-20, К-21); высота потолка 2700 мм принята, источника нет (К-24); тип дома и перекрытие (монолит, плита 220 мм) приняты, источника нет (К-3); толщины стен приняты (250 и 120 мм), источника нет (К-21); мощность 15 кВт принята, технических условий нет (К-25).

Знак «**» — предложение проектировщика, заказчиком не утверждено (согласовать с заказчиком): ИЗ-4: S2 — светорегулятор добавлен под диммируемую ленту L3; уровни сценариев выбраны конвейером.

См. лист открытых вопросов (лист 6, запись К-3; лист 7, записи К-20, К-21, К-24, К-25; лист 9, запись ИЗ-4; лист 10, запись ИЗ-8).

Примечания

1. Развёртки — вид на стену изнутри помещения, по часовой стрелке; расположение — на схеме листа и на листе 90; размеры — в мм по чистовым поверхностям; отметки — в м от ±0,000; высоты H — от чистого пола помещения до оси изделия, у декора — до центра.
2. Красные цепочки — привязки электроточек и выводов: по горизонтали от угла чистовых стен, по вертикали от чистого пола, до оси изделия; звенья короче 3 мм на листе вынесены во второй ярус (ближняя к стене цепочка).
3. У знака электроточки: марка (Р — розетка, S — выключатель, Св — светильник, ЭВ — вывод кабеля), ×N — число постов в рамке, гр. — группа щита, H — высота оси от чистого пола, мм; группы по клавишам выключателя — на листе выключателей.
4. Схема мебели, приборов и декора не является технической документацией для производства мебели; габариты — по паспортам изделий.
5. Картины и зеркала крепить к основанию по паспорту изделия (закладные и анкеры — в перечне скрытых работ); крест — ось центра предмета.
6. Карнизы (шины) — по ведомости текстиля декоратора; длина L и верх H — по развёртке, крепление — до окраски потолка.
7. Потолок на развёртках — по нижнему уровню У1; другие уровни потолка помещения: У2 +2,600.
8. Линии узора (швы плитки, складки штор, рёбра радиаторов) прерываются у знаков и выносок — просвет между линиями не менее 0,7 мм.

1000 мм · печать 1:1

Изм.	Кол.уч	Лист	№ док.	Подп.	Дата
Разраб.		Кырлан А.С.			21.10.26
Пров.					
ГИП		Кырлан А.С.			21.10.26
Н. контр.					
Утв.					

ГД-2026-004-АИ

Четырёхкомнатная квартира

Общая площадь 102,67* м² · * размеры со скана, не замерены (реестр — л. 6–11, ИЗ-8, К-20, К-21)

Дизайн-проект интерьера четырёхкомнатной квартиры

Стадия	Лист	Листов
РП	92	124

Развёртки стен В, Г. Зал (пом. 1)

М 1:40

Кырлан Александр Сергеевич

выпуск 05.10.2026 № 7e7a2cd217 · стр. 103 из 168

Развёртка стены А. Ванная комната (пом. 2)

Ванная комната (пом. 2) · вид изнутри помещения · размеры в мм, отметки в м

ПРЕДВАРИТЕЛЬНО · не для производства работ · открыто пунктов: 30 (реестр — л. 6–11)

Развёртка стены А

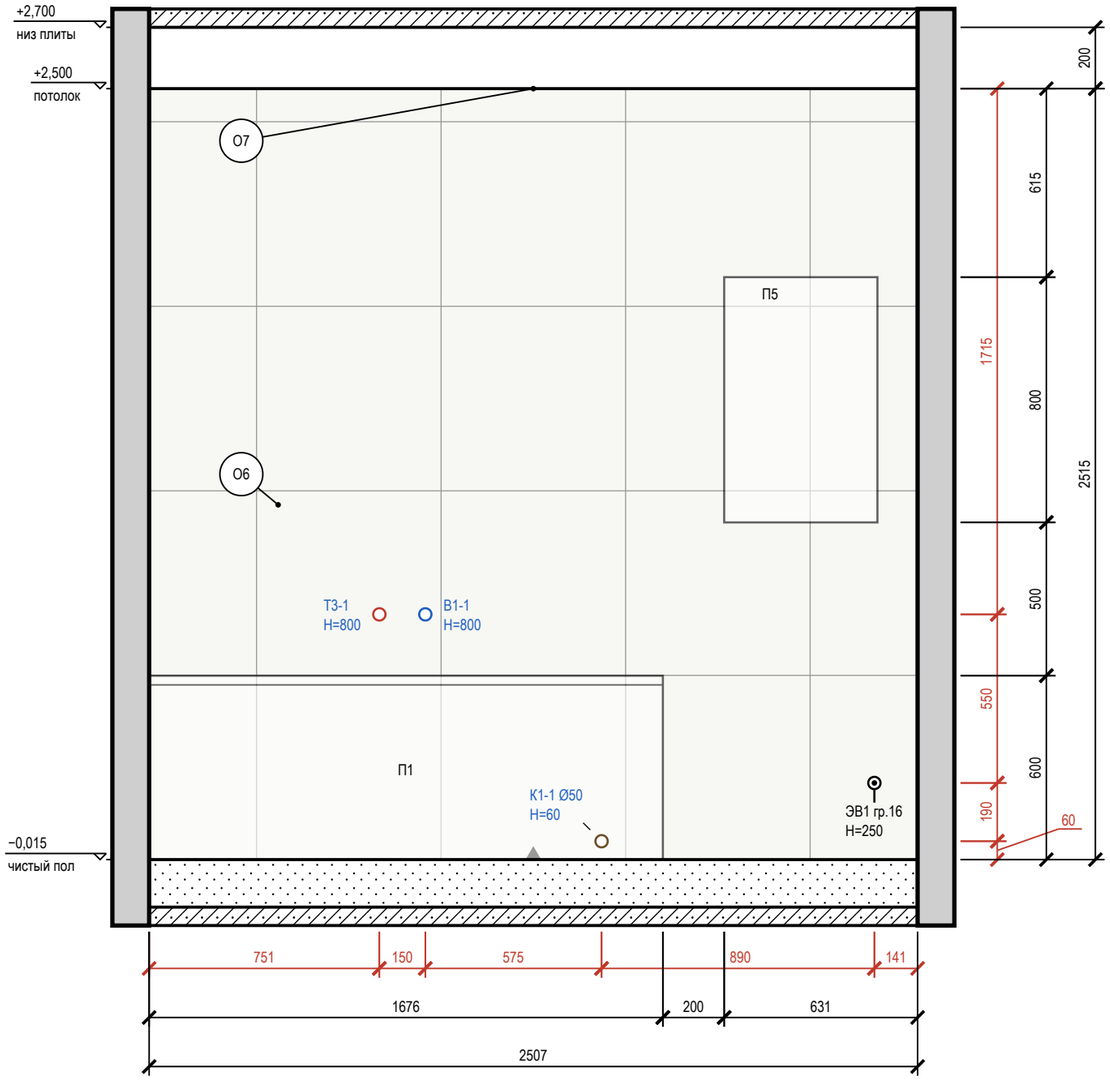

Схема развёрток (М 1:100)

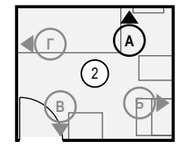

Условные обозначения

- вывод кабеля для подключения прибора (без розетки), марка ЭВ
- вывод В1 (код — в ведомости привязок)
- вывод Т3 (код — в ведомости привязок)
- вывод К1 (код — в ведомости привязок)
- привязки точек и выводов от угла и от пола, мм
- мебель и приборы — фасад по расстановке (условно)
- стены и перекрытия в сечении
- плитка: сетка швов по формату, ▲ — ось старта
- окраска: тон — цвет по коду производителя (условно)
- О1 — марка отделки по реестру отделки альбома
- А — марка развёртки: буква стены, стрелка — взгляд

Ведомость отделки (на листе)

Марка	Поверхность	Материал, изделие	Цвет, код	Кол.
О6	стены	облицовка плиткой, 600×600×9 мм, аналог: керамогранит матовый, тон F497, затирка CG2WA	#F1F1EC «тон Paper F497»	6,3 м²
О7	потолок	окраска, Tikkurila Luja 7, матовая, подготовка Q3	Tikkurila F497 «Paper»	5,6 м²

Допущения и предложения на листе

Основа листа: размеры сняты с размерных цепочек растрового скана плана заказчика, на объекте не замерены; ступени наружного контура приведены к граням помещений модели (ИЗ-8, К-20, К-21); высота потолка 2700 мм принята, источника нет (К-24); тип дома и перекрытие (монолит, плита 220 мм) приняты, источника нет (К-3); толщины стен приняты (250 и 120 мм), источника нет (К-21); мощность 15 кВт принята, технических условий нет (К-25).

Знак «**» — предложение проектировщика, заказчиком не утверждено (согласовать с заказчиком): ИЗ-8: дверь пом. 2 (стена В) — смещение 100 → 110 мм (откос до угла был 40 мм при норме от 50 мм).

См. лист открытых вопросов (лист 6, запись К-3; лист 7, записи К-20, К-21, К-24, К-25; лист 10, запись ИЗ-8).

Примечания

1. Развёртки — вид на стену изнутри помещения, по часовой стрелке; расположение — на схеме листа и на листе 90; размеры — в мм по чистовым поверхностям; отметки — в м от ±0,000; высоты Н — от чистого пола помещения до оси изделия, у декора — до центра.
2. Красные цепочки — привязки электроточек и выводов: по горизонтали от угла чистовых стен, по вертикали от чистого пола, до оси изделия; звенья короче 3 мм на листе вынесены во второй ярус (ближняя к стене цепочка).
3. У знака электроточки: марка (Р — розетка, S — выключатель, Св — светильник, ЭВ — вывод кабеля), ×N — число постов в рамке, гр. — группа щита, Н — высота оси от чистого пола, мм; группы по клавишам выключателя — на листе выключателей.
4. Схема мебели, приборов и декора не является технической документацией для производства мебели; габариты — по паспортам изделий.
5. Облицовка — по сетке швов 2 мм, раскладка от оси стены (треугольник у пола); подрезки — по листу раскладки плитки.
6. Гидроизоляция в 2 слоя, заход на стены 200 мм, в зоне душа — 2100 мм — до облицовки, с актом скрытых работ и тестом проливом (узел — на листе узлов).

1000 мм · печать 1:1

Изм.	Кол.уч	Лист	№ док.	Подп.	Дата
Разраб.		Кырлан А.С.			21.10.26
Пров.					
ГИП		Кырлан А.С.			21.10.26
Н. контр.					
Утв.					

ГД-2026-004-АИ

Четырёхкомнатная квартира

Общая площадь 102,67* м² · * размеры со скана, не замерены (реестр — л. 6–11, ИЗ-8, К-20, К-21)

Дизайн-проект интерьера четырёхкомнатной квартиры

Стадия	Лист	Листов
РП	93	124

Развёртка стены А. Ванная комната (пом. 2)

М 1:20

Кырлан Александр Сергеевич

выпуск 05.10.2026 № 7e7a2cd217 · стр. 104 из 168

Развёртка стены Б. Ванная комната (пом. 2)

Ванная комната (пом. 2) · вид изнутри помещения · размеры в мм, отметки в м

ПРЕДВАРИТЕЛЬНО · не для производства работ · открыто пунктов: 30 (реестр — л. 6–11)

Развёртка стены Б

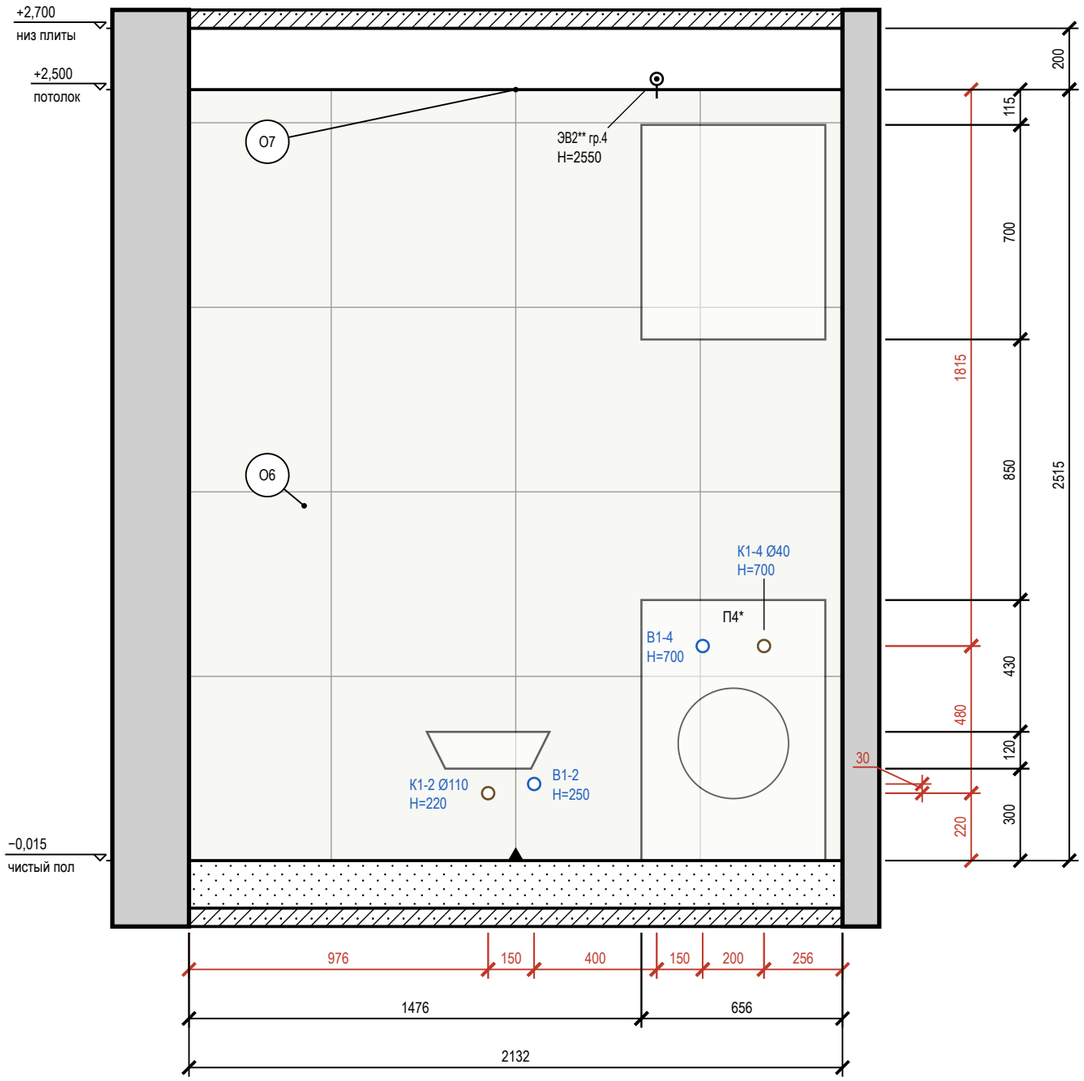

Схема развёрток (М 1:100)

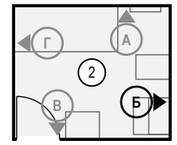

Условные обозначения

- вывод кабеля для подключения прибора (без розетки), марка ЭВ
- вывод В1 (код — в ведомости привязок)
- вывод К1 (код — в ведомости привязок)
- привязки точек и выводов от угла и от пола, мм
- мебель и приборы — фасад по расстановке (условно)
- стены и перекрытия в сечении
- плитка: сетка швов по формату, ▲ — ось старта
- окраска: тон — цвет по коду производителя (условно)
- О1 — марка отделки по реестру отделки альбома
- А — марка развёртки: буква стены, стрелка — взгляд

Ведомость отделки (на листе)

Марка	Поверхность	Материал, изделие	Цвет, код	Кол.
О6	стены	облицовка плиткой, 600×600×9 мм, аналог: керамогранит матовый, тон F497, затирка CG2WA	#F1F1EC «тон Paper F497»	5,4 м²
О7	потолок	окраска, Tikkurila Luja 7, матовая, подготовка Q3	Tikkurila F497 «Paper»	5,6 м²

Допущения и предложения на листе

Основа листа: размеры сняты с размерных цепочек растрового скана плана заказчика, на объекте не замерены; ступени наружного контура приведены к граням помещений модели (ИЗ-8, К-20, К-21); высота потолка 2700 мм принята, источника нет (К-24); тип дома и перекрытие (монолит, плита 220 мм) приняты, источника нет (К-3); толщины стен приняты (250 и 120 мм), источника нет (К-21); мощность 15 кВт принята, технических условий нет (К-25).

Знак «**» — предложение проектировщика, заказчиком не утверждено (согласовать с заказчиком): ИЗ-8: дверь пом. 2 (стена В) — смещение 100 → 110 мм (откос до угла был 40 мм при норме от 50 мм); ИЗ-12: ЭВ2 — вывод к бытовому вентилятору, таймер выбега.

См. лист открытых вопросов (лист 6, запись К-3; лист 7, записи К-20, К-21, К-24, К-25; лист 10, записи ИЗ-8, ИЗ-12).

Примечания

1. Развёртки — вид на стену изнутри помещения, по часовой стрелке; расположение — на схеме листа и на листе 90; размеры — в мм по чистовым поверхностям; отметки — в м от ±0,000; высоты H — от чистого пола помещения до оси изделия, у декора — до центра.
2. Красные цепочки — привязки электроточек и выводов: по горизонтали от угла чистовых стен, по вертикали от чистого пола, до оси изделия; звенья короче 3 мм на листе вынесены во второй ярус (ближняя к стене цепочка).
3. У знака электроточки: марка (Р — розетка, S — выключатель, Св — светильник, ЭВ — вывод кабеля), ×N — число постов в рамке, гр. — группа щита, H — высота оси от чистого пола, мм; группы по клавишам выключателя — на листе выключателей.
4. Схема мебели, приборов и декора не является технической документацией для производства мебели; габариты — по паспортам изделий (* — высота не задана в проекте, показана по типовому изделию).
5. Облицовка — по сетке швов 2 мм, раскладка от оси стены (треугольник у пола); подрезки — по листу раскладки плитки.
6. Гидроизоляция в 2 слоя, заход на стены 200 мм, в зоне душа — 2100 мм — до облицовки, с актом скрытых работ и тестом проливом (узел — на листе узлов).

1000 мм · печать 1:1

Изм.	Кол.уч	Лист	№ док.	Подп.	Дата
Разраб.		Кырлан А.С.			21.10.26
Пров.					
ГИП		Кырлан А.С.			21.10.26
Н. контр.					
Утв.					

ГД-2026-004-АИ

Четырёхкомнатная квартира

Общая площадь 102,67* м² · * размеры со скана, не замерены (реестр — л. 6–11, ИЗ-8, К-20, К-21)

Дизайн-проект интерьера четырёхкомнатной квартиры

Стадия	Лист	Листов
РП	94	124

Развёртка стены Б. Ванная комната (пом. 2)

М 1:20

Кырлан Александр Сергеевич

выпуск 05.10.2026 № 7e7a2cd217 · стр. 105 из 168

Развёртка стены В. Ванная комната (пом. 2)

Ванная комната (пом. 2) · вид изнутри помещения · размеры в мм, отметки в м

ПРЕДВАРИТЕЛЬНО · не для производства работ · открыто пунктов: 30 (реестр — л. 6–11)

Развёртка стены В

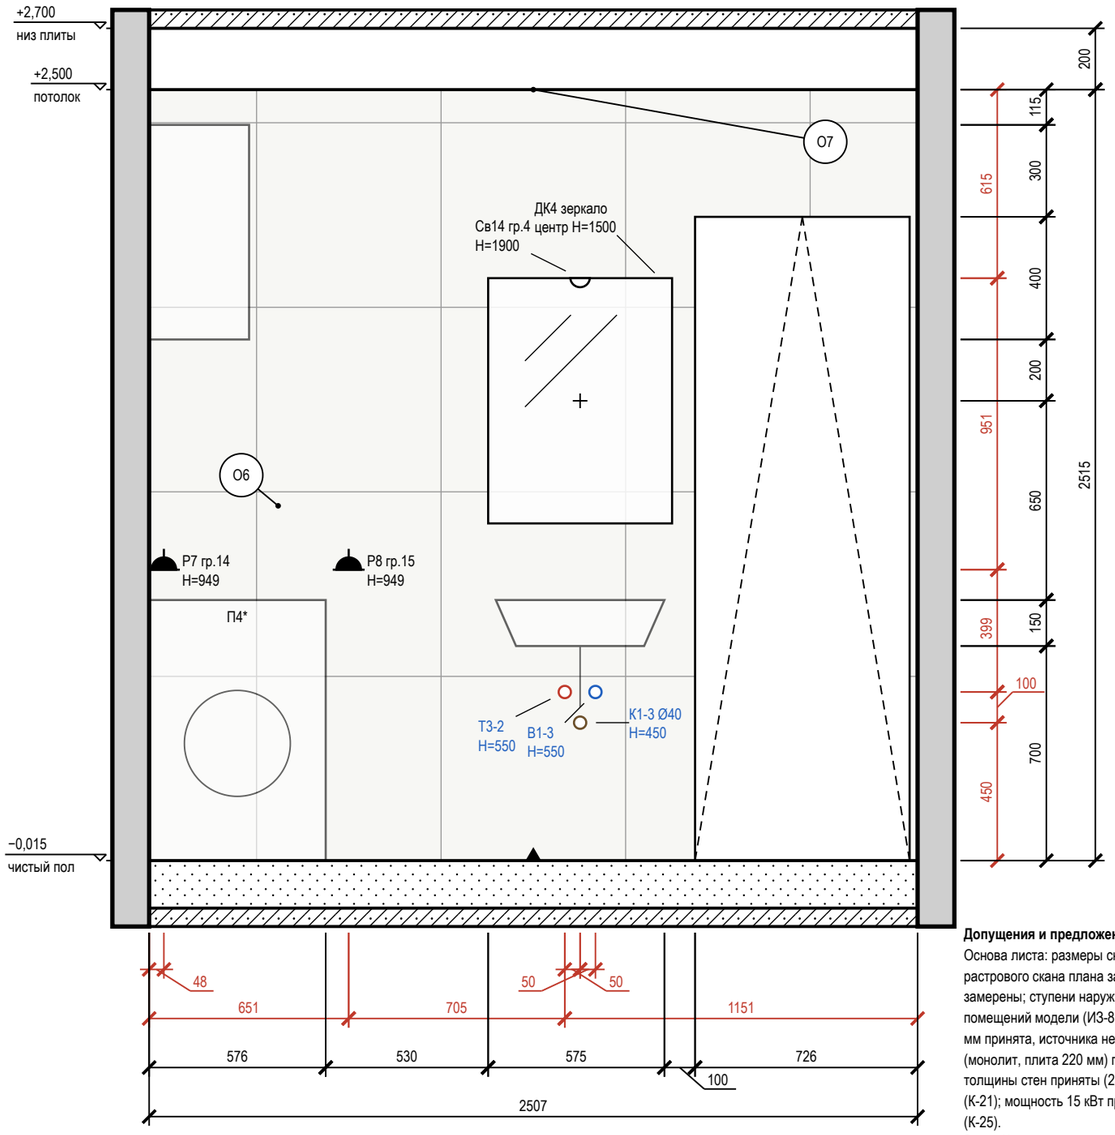

Схема развёрток (М 1:100)

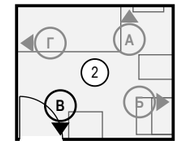

Условные обозначения

- розетка влагозащищённая IP44
- светильник настенный (бра), Н — высота оси
- вывод В1 (код — в ведомости привязок)
- вывод Т3 (код — в ведомости привязок)
- вывод К1 (код — в ведомости привязок)
- привязки точек и выводов от угла и от пола, мм
- мебель и приборы — фасад по расстановке (условно)
- зеркало: марка Д, крест — центр, Н — высота центра, мм
- дверной проём; марка двери — в кружке
- стены и перекрытия в сечении
- плитка: сетка швов по формату, ▲ — ось старта
- окраска: тон — цвет по коду производителя (условно)
- О1 — марка отделки по реестру отделки альбома
- А — марка развёртки: буква стены, стрелка — взгляд

Ведомость отделки (на листе)

Марка	Поверхность	Материал, изделие	Цвет, код	Кол.
О6	стены	облицовка плиткой, 600×600×9 мм, аналог: керамогранит матовый, тон F497, затирка CG2WA	#F1F1EC «тон Paper F497»	4,8 м²
О7	потолок	окраска, Tikkurila Luja 7, матовая, подготовка Q3	Tikkurila F497 «Paper»	5,6 м²

Допущения и предложения на листе

Основа листа: размеры сняты с размерных цепочек растрового скана плана заказчика, на объекте не замерены; ступени наружного контура приведены к граням помещений модели (ИЗ-8, К-20, К-21); высота потолка 2700 мм принята, источника нет (К-24); тип дома и перекрытие (монолит, плита 220 мм) приняты, источника нет (К-3); толщины стен приняты (250 и 120 мм), источника нет (К-21); мощность 15 кВт принята, технических условий нет (К-25).

Знак «**» — предложение проектировщика, заказчиком не утверждено (согласовать с заказчиком): ИЗ-8: дверь пом. 2 (стена В) — смещение 100 → 110 мм (откос до угла был 40 мм при норме от 50 мм).

См. лист открытых вопросов (лист 6, запись К-3; лист 7, записи К-20, К-21, К-24, К-25; лист 10, запись ИЗ-8).

Примечания

1. Развёртки — вид на стену изнутри помещения, по часовой стрелке; расположение — на схеме листа и на листе 90; размеры — в мм по чистовым поверхностям; отметки — в м от ±0,000; высоты Н — от чистого пола помещения до оси изделия, у декора — до центра.
2. Красные цепочки — привязки электроточек и выводов: по горизонтали от угла чистовых стен, по вертикали от чистого пола, до оси изделия; звенья короче 3 мм на листе вынесены во второй ярус (ближняя к стене цепочка).
3. У знака электроточки: марка (Р — розетка, S — выключатель, Св — светильник, ЭВ — вывод кабеля), ×N — число постов в рамке, гр. — группа щита, Н — высота оси от чистого пола, мм; группы по клавишам выключателя — на листе выключателей.
4. Схема мебели, приборов и декора не является технической документацией для производства мебели; габариты — по паспортам изделий (* — высота не задана в проекте, показана по типовому изделию).
5. Облицовка — по сетке швов 2 мм, раскладка от оси стены (треугольник у пола); подрезки — по листу раскладки плитки.
6. Гидроизоляция в 2 слоя, заход на стены 200 мм, в зоне душа — 2100 мм — до облицовки, с актом скрытых работ и тестом проливом (узел — на листе узлов).
7. Картины и зеркала крепить к основанию по паспорту изделия (закладные и анкеры — в перечне скрытых работ); крест — ось центра предмета.

1000 мм · печать 1:1

Изм.	Кол.уч	Лист	№ док.	Подп.	Дата
Разраб.		Кырлан А.С.			21.10.26
Пров.					
ГИП		Кырлан А.С.			21.10.26
Н. контр.					
Утв.					

ГД-2026-004-АИ

Четырёхкомнатная квартира

Общая площадь 102,67* м² · * размеры со скана, не замерены (реестр — л. 6–11, ИЗ-8, К-20, К-21)

Дизайн-проект интерьера четырёхкомнатной квартиры

Стадия	Лист	Листов
РП	95	124

Развёртка стены В. Ванная комната (пом. 2)

М 1:20

Кырлан Александр Сергеевич

выпуск 05.10.2026 № 7e7a2cd217 · стр. 106 из 168

Развёртка стены Г. Ванная комната (пом. 2)

Ванная комната (пом. 2) · вид изнутри помещения · размеры в мм, отметки в м

ПРЕДВАРИТЕЛЬНО · не для производства работ · открыто пунктов: 30 (реестр — л. 6–11)

Развёртка стены Г

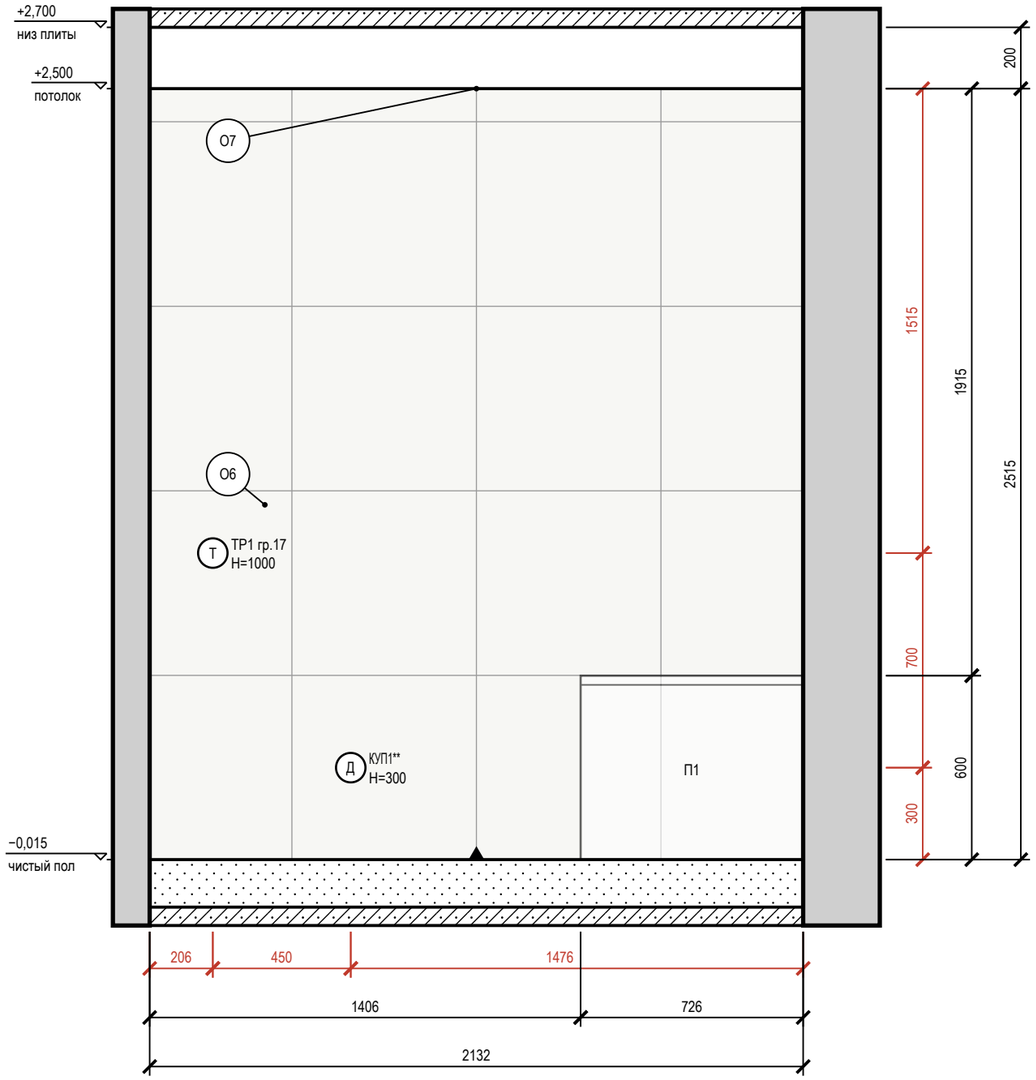

Допущения и предложения на листе

Основа листа: размеры сняты с размерных цепочек растрового скана плана заказчика, на объекте не замерены; ступени наружного контура приведены к граням помещений модели (ИЗ-8, К-20, К-21); высота потолка 2700 мм принята, источника нет (К-24); тип дома и перекрытие (монолит, плита 220 мм) приняты, источника нет (К-3); толщины стен приняты (250 и 120 мм), источника нет (К-21); мощность 15 кВт принята, технических условий нет (К-25).

Знак «**» — предложение проектировщика, заказчиком не утверждено (согласовать с заказчиком): ИЗ-8: дверь пом. 2 (стена В) — смещение 100 → 110 мм (откос до угла был 40 мм при норме от 50 мм); ИЗ-12: КУП1 — коробка уравнивания потенциалов, проводник от шины РЕ.

См. лист открытых вопросов (лист 6, запись К-3; лист 7, записи К-20, К-21, К-24, К-25; лист 10, записи ИЗ-8, ИЗ-12).

Примечания

1. Развёртки — вид на стену изнутри помещения, по часовой стрелке; расположение — на схеме листа и на листе 90; размеры — в мм по чистовым поверхностям; отметки — в м от ±0,000; высоты Н — от чистого пола помещения до оси изделия, у декора — до центра.
2. Красные цепочки — привязки электроточек и выводов: по горизонтали от угла чистовых стен, по вертикали от чистого пола, до оси изделия; звенья короче 3 мм на листе вынесены во второй ярус (ближняя к стене цепочка).
3. У знака электроточки: марка (Р — розетка, S — выключатель, Св — светильник, ЭВ — вывод кабеля), ×N — число постов в рамке, гр. — группа щита, Н — высота оси от чистого пола, мм; группы по клавишам выключателя — на листе выключателей.
4. Схема мебели, приборов и декора не является технической документацией для производства мебели; габариты — по паспортам изделий.
5. Облицовка — по сетке швов 2 мм, раскладка от оси стены (треугольник у пола); подрезки — по листу раскладки плитки.
6. Гидроизоляция в 2 слоя, заход на стены 200 мм, в зоне душа — 2100 мм — до облицовки, с актом скрытых работ и тестом проливом (узел — на листе узлов).

1000 мм · печать 1:1

Схема развёрток (М 1:100)

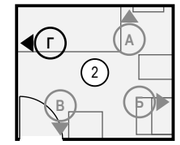

Условные обозначения

- Т — терморегулятор тёплого пола
- привязки точек и выводов от угла и от пола, мм
- мебель и приборы — фасад по расстановке (условно)
- стены и перекрытия в сечении
- плитка: сетка швов по формату, ▲ — ось старта
- окраска: тон — цвет по коду производителя (условно)
- О1 — марка отделки по реестру отделки альбома
- А — марка развёртки: буква стены, стрелка — взгляд

Ведомость отделки (на листе)

Марка	Поверхность	Материал, изделие	Цвет, код	Кол.
О6	стены	облицовка плиткой, 600×600×9 мм, аналог: керамогранит матовый, тон F497, затирка CG2WA	#F1F1EC «тон Paper F497»	5,4 м²
О7	потолок	окраска, Tikkurila Luja 7, матовая, подготовка Q3	Tikkurila F497 «Paper»	5,6 м²

Изм.	Кол.уч	Лист	№ док.	Подп.	Дата
Разраб.		Кырлан А.С.			21.10.26
Пров.					
ГИП		Кырлан А.С.			21.10.26
Н. контр.					
Утв.					

ГД-2026-004-АИ

Четырёхкомнатная квартира

Общая площадь 102,67* м² · * размеры со скана, не замерены (реестр — л. 6–11, ИЗ-8, К-20, К-21)

Дизайн-проект интерьера четырёхкомнатной квартиры

Стадия	Лист	Листов
РП	96	124

Развёртка стены Г. Ванная комната (пом. 2)

М 1:20

Кырлан Александр Сергеевич

выпуск 05.10.2026 № 7e7a2cd217 · стр. 107 из 168

Развёртки стен. Тёмная комната (пом. 3)

Тёмная комната (пом. 3) · вид изнутри помещения · размеры в мм, отметки в м

ПРЕДВАРИТЕЛЬНО · не для производства работ · открыто пунктов: 30 (реестр — л. 6–11)

Развёртка стены А

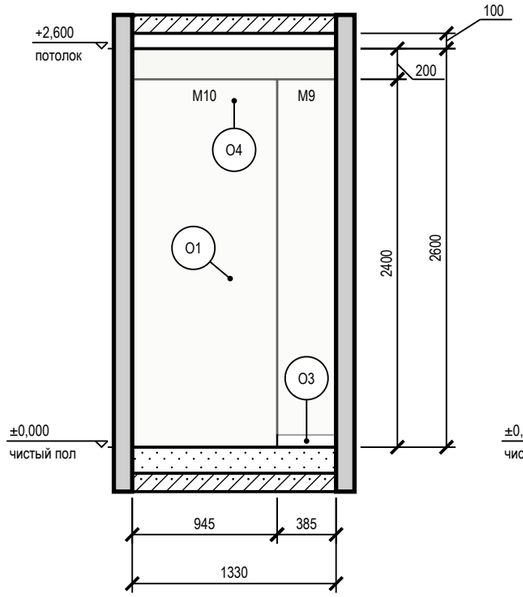

Развёртка стены Б

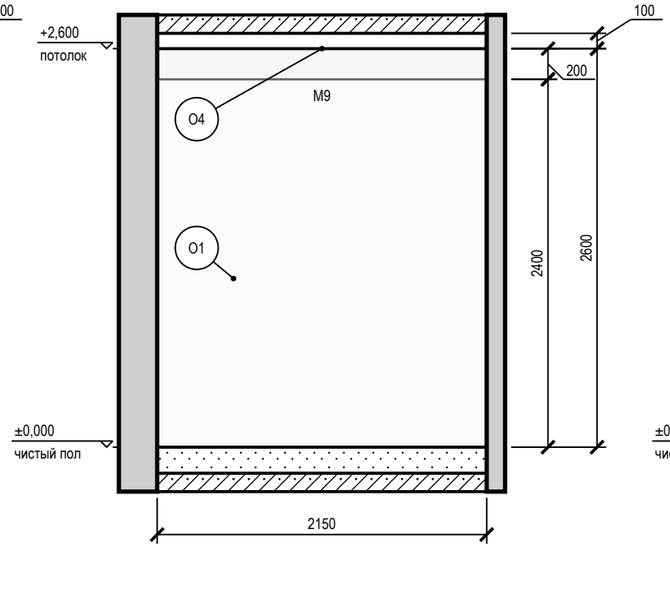

Развёртка стены В

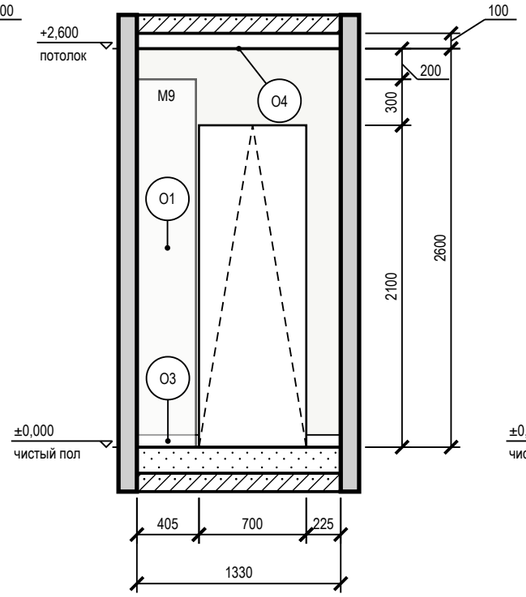

Развёртка стены Г

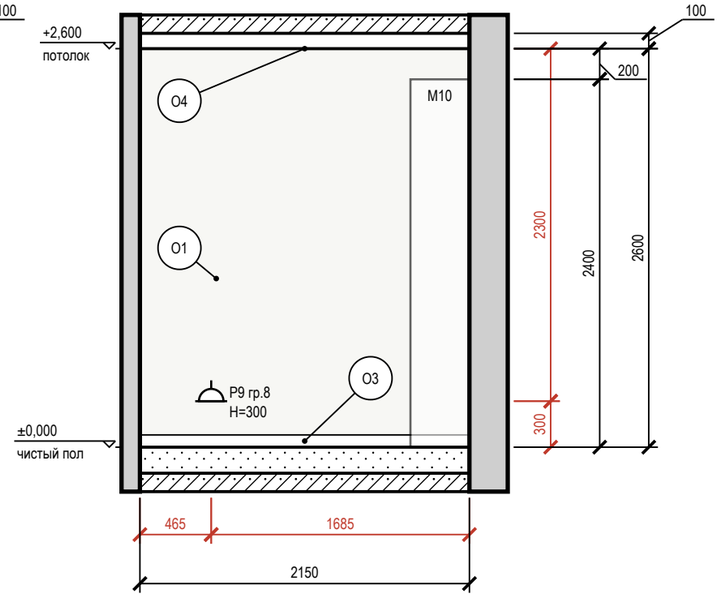

Схема развёрток (М 1:100)

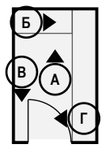

Условные обозначения

- розетка с заземляющим контактом; у знака — марка, ×N постов в рамке, гр. — группа щита, H — высота оси, мм
- привязки точек и выводов от угла и от пола, мм
- мебель и приборы — фасад по расстановке (условно)
- дверной проём; марка двери — в кружке
- стены и перекрытия в сечении
- окраска: тон — цвет по коду производителя (условно)
- O1 — марка отделки по реестру отделки альбома
- А — марка развёртки: буква стены, стрелка — взгляд

Ведомость отделки (на листе)

Марка	Поверхность	Материал, изделие	Цвет, код	Кол.
O1	стены	окраска, Tikkurila Optiva 5 Matt, матовая, подготовка К3	Tikkurila F497 «Paper»	16,6 м²
O3	плинтус	плинтус МДФ, h 80 мм, аналог: плинтус МДФ под окраску 80×16 мм, полуглянцевая	Tikkurila F497 «Paper»	3,2 м
O4	потолок	окраска, Tikkurila Anti-Reflex 2, глубокоматовая, подготовка Q3	Tikkurila F497 «Paper»	3 м²

Допущения и предложения на листе

Основа листа: размеры сняты с размерных цепочек растрового скана плана заказчика, на объекте не замерены; ступени наружного контура приведены к граням помещений модели (ИЗ-8, К-20, К-21); высота потолка 2700 мм принята, источника нет (К-24); тип дома и перекрытие (монолит, плита 220 мм) приняты, источника нет (К-3); толщины стен приняты (250 и 120 мм), источника нет (К-21); мощность 15 кВт принята, технических условий нет (К-25).

См. лист открытых вопросов (лист 6, запись К-3; лист 7, записи К-20, К-21, К-24, К-25; лист 10, запись ИЗ-8).

Примечания

1. Развёртки — вид на стену изнутри помещения, по часовой стрелке; расположение — на схеме листа и на листе 90; размеры — в мм по чистовым поверхностям; отметки — в м от ±0,000; высоты H — от чистого пола помещения до оси изделия, у декора — до центра.
2. Красные цепочки — привязки электроточек и выводов: по горизонтали от угла чистовых стен, по вертикали от чистого пола, до оси изделия; звенья короче 3 мм на листе вынесены во второй ярус (ближняя к стене цепочка).
3. У знака электроточки: марка (Р — розетка, S — выключатель, Св — светильник, ЭВ — вывод кабеля), ×N — число постов в рамке, гр. — группа щита, H — высота оси от чистого пола, мм; группы по клавишам выключателя — на листе выключателей.
4. Схема мебели, приборов и декора не является технической документацией для производства мебели; габариты — по паспортам изделий.

1000 мм · печать 1:1

Изм.	Кол.уч	Лист	№ док.	Подп.	Дата
Разраб.		Кырлан А.С.			21.10.26
Пров.					
ГИП		Кырлан А.С.			21.10.26
Н. контр.					
Утв.					

ГД-2026-004-АИ

Четырёхкомнатная квартира

Общая площадь 102,67* м² · * размеры со скана, не замерены (реестр — л. 6–11, ИЗ-8, К-20, К-21)

Дизайн-проект интерьера четырёхкомнатной квартиры

Стадия	Лист	Листов
РП	97	124

Развёртки стен. Тёмная комната (пом. 3)

М 1:40

Кырлан Александр Сергеевич

выпуск 05.10.2026 № 7e7a2cd217 · стр. 108 из 168

Развёртки стен А, Б. Детская 1 (пом. 4)

Детская 1 (пом. 4) · вид изнутри помещения · размеры в мм, отметки в м

ПРЕДВАРИТЕЛЬНО · не для производства работ · открыто пунктов: 30 (реестр — л. 6–11)

Развёртка стены А

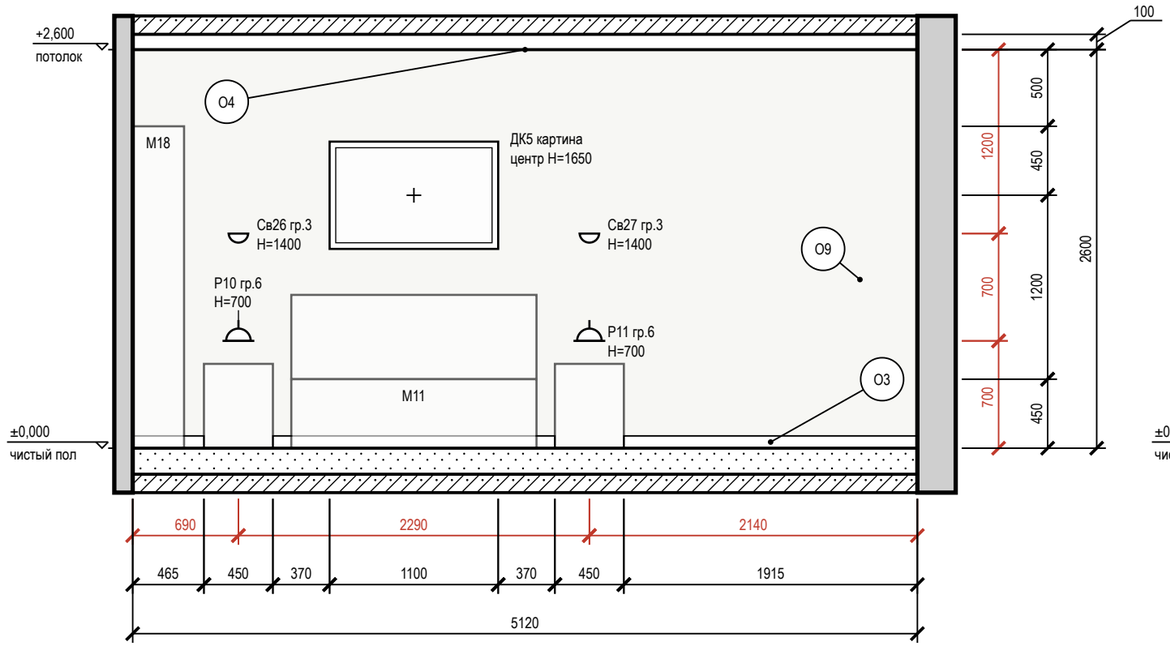

Развёртка стены Б

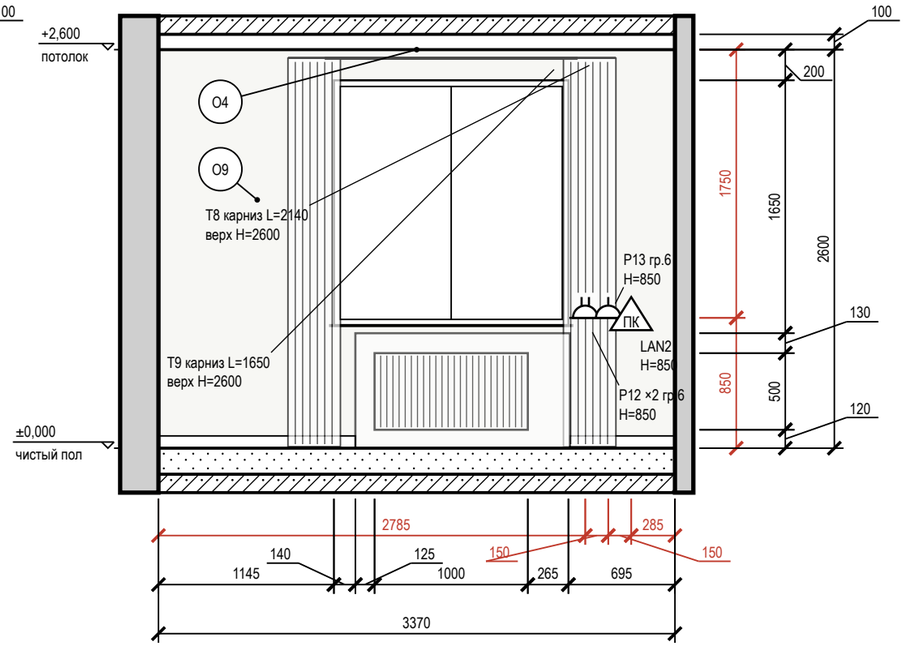

Схема развёрток (М 1:100)

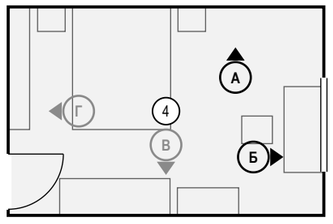

Условные обозначения

- розетка с заземляющим контактом; у знака — марка, ×N постов в рамке, гр. — группа щита, Н — высота оси, мм
- светильник настенный (бра), Н — высота оси
- ПК — розетка компьютерная RJ45
- привязки точек и выводов от угла и от пола, мм
- мебель и приборы — фасад по расстановке (условно)
- картина (декор): марка Д, крест — центр, Н — высота центра, мм
- карниз (шина) и шторы в собранном виде: марка Т, длина L, верх Н
- окно: проём, рама, подоконник
- радиатор отопления; марка — по плану отопления
- стены и перекрытия в сечении
- окраска: тон — цвет по коду производителя (условно)
- О1 — марка отделки по реестру отделки альбома
- А — марка развёртки: буква стены, стрелка — взгляд

Ведомость отделки (на листе)

Марка	Поверхность	Материал, изделие	Цвет, код	Кол.
О3	плинтус	плинтус МДФ, h 80 мм, аналог: плинтус МДФ под окраску 80×16 мм, полуглянцевая	Tikkurila F497 «Paper»	6,2 м
О4	потолок	окраска, Tikkurila Anti-Reflex 2, глубокоматовая, подготовка Q3	Tikkurila F497 «Paper»	17,5 м²
О9	стены	окраска, Tikkurila Joker, шелковисто-матовая, подготовка К3	Tikkurila F497 «Paper»	19,6 м²

Допущения и предложения на листе

Основа листа: размеры сняты с размерных цепочек растрового скана плана заказчика, на объекте не замерены; ступени наружного контура приведены к граням помещений модели (И3-8, К-20, К-21); высота потолка 2700 мм принята, источника нет (К-24); тип дома и перекрытие (монолит, плита 220 мм) приняты, источника нет (К-3); толщины стен приняты (250 и 120 мм), источника нет (К-21); мощность 15 кВт принята, технических условий нет (К-25).

См. лист открытых вопросов (лист 6, запись К-3; лист 7, записи К-20, К-21, К-24, К-25; лист 10, запись И3-8).

Примечания

1. Развёртки — вид на стену изнутри помещения, по часовой стрелке; расположение — на схеме листа и на листе 90; размеры — в мм по чистовым поверхностям; отметки — в м от ±0,000; высоты Н — от чистого пола помещения до оси изделия, у декора — до центра.
2. Красные цепочки — привязки электроточек и выводов: по горизонтали от угла чистовых стен, по вертикали от чистого пола, до оси изделия; звенья короче 3 мм на листе вынесены во второй ярус (ближняя к стене цепочка).
3. У знака электроточки: марка (Р — розетка, S — выключатель, Св — светильник, ЭВ — вывод кабеля), ×N — число постов в рамке, гр. — группа щита, Н — высота оси от чистого пола, мм; группы по клавишам выключателя — на листе выключателей.
4. Схема мебели, приборов и декора не является технической документацией для производства мебели; габариты — по паспортам изделий.
5. Картины и зеркала крепить к основанию по паспорту изделия (закладные и анкеры — в перечне скрытых работ); крест — ось центра предмета.
6. Карнизы (шины) — по ведомости текстиля декоратора; длина L и верх Н — по развёртке, крепление — до окраски потолка.
7. Линии узора (швы плитки, складки штор, рёбра радиаторов) прерываются у знаков и выносок — просвет между линиями не менее 0,7 мм.

1000 мм · печать 1:1

Изм.	Кол.уч	Лист	№ док.	Подп.	Дата
Разраб.		Кырлан А.С.			21.10.26
Пров.					
ГИП		Кырлан А.С.			21.10.26
Н. контр.					
Утв.					

ГД-2026-004-АИ

Четырёхкомнатная квартира

Общая площадь 102,67* м² · * размеры со скана, не замерены (реестр — л. 6–11, И3-8, К-20, К-21)

Дизайн-проект интерьера четырёхкомнатной квартиры

Стадия	Лист	Листов
РП	98	124

Развёртки стен А, Б. Детская 1 (пом. 4)

М 1:40

Кырлан Александр Сергеевич

выпуск 05.10.2026 № 7e7a2cd217 · стр. 109 из 168

Развёртки стен В, Г. Детская 1 (пом. 4)

Детская 1 (пом. 4) · вид изнутри помещения · размеры в мм, отметки в м

ПРЕДВАРИТЕЛЬНО · не для производства работ · открыто пунктов: 30 (реестр — л. 6–11)

Развёртка стены В

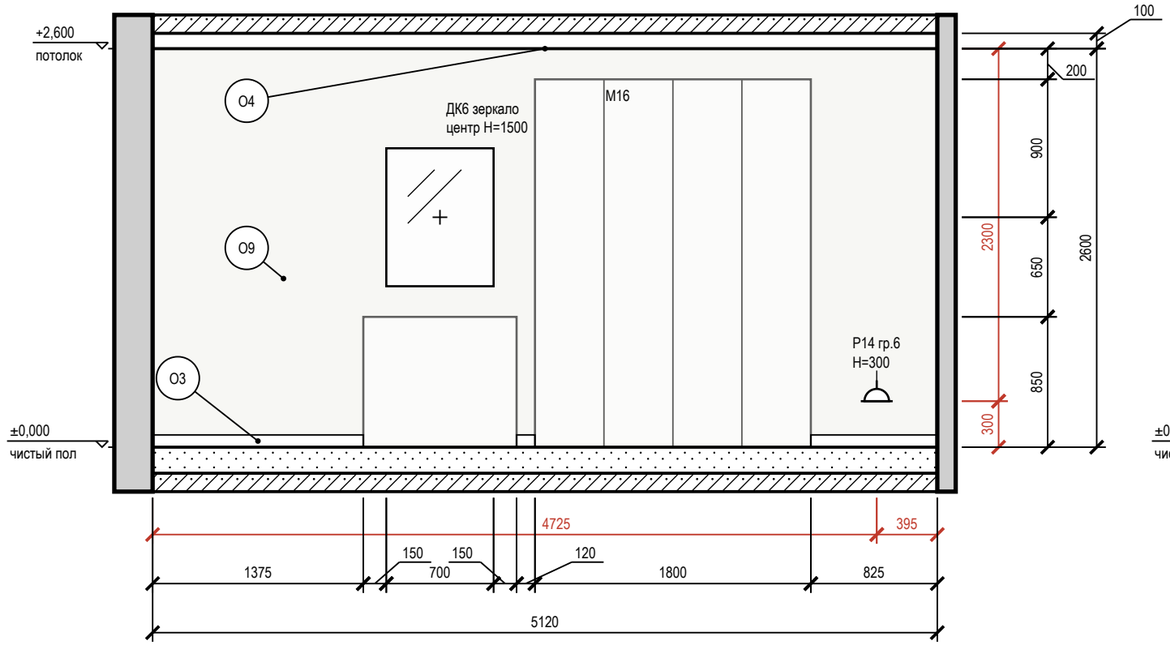

Развёртка стены Г

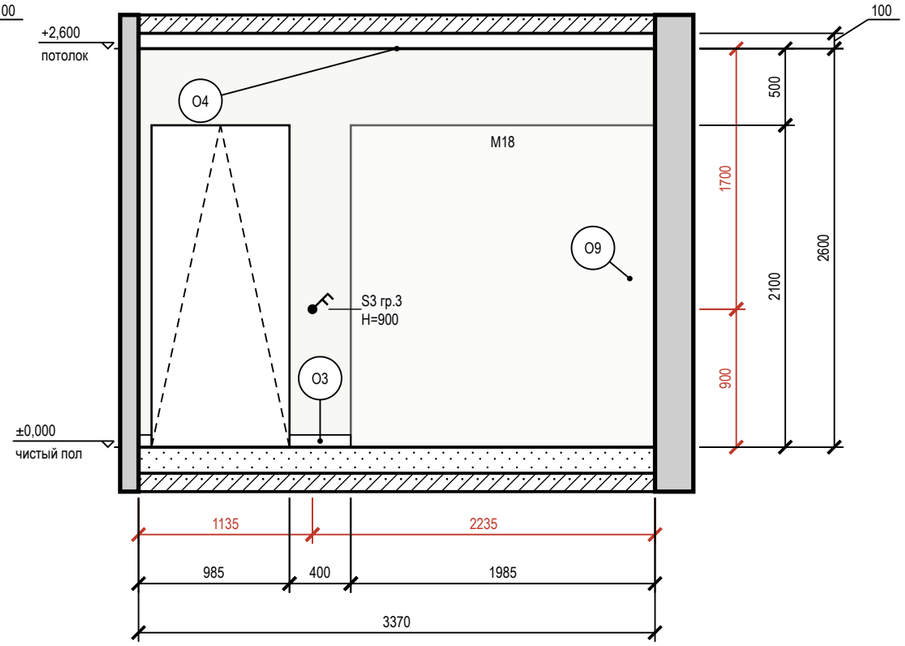

Схема развёрток (М 1:100)

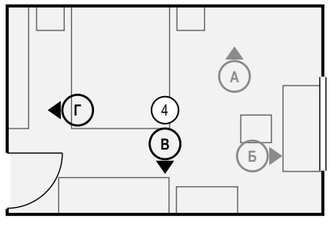

Условные обозначения

- розетка с заземляющим контактом; у знака — марка, ×N постов в рамке, гр. — группа щита, Н — высота оси, мм
- выключатель одноклавишный
- выключатель двухклавишный (флажков — по числу клавиш)
- привязки точек и выводов от угла и от пола, мм
- мебель и приборы — фасад по расстановке (условно)
- зеркало: марка Д, крест — центр, Н — высота центра, мм
- дверной проём; марка двери — в кружке
- стены и перекрытия в сечении
- окраска: тон — цвет по коду производителя (условно)
- О1 — марка отделки по реестру отделки альбома
- А — марка развёртки: буква стены, стрелка — взгляд

Ведомость отделки (на листе)

Марка	Поверхность	Материал, изделие	Цвет, код	Кол.
О3	плинтус	плинтус МДФ, h 80 мм, аналог: плинтус МДФ под окраску 80×16 мм, полуглянцевая	Tikkurila F497 «Paper»	2,8 м
О4	потолок	окраска, Tikkurila Anti-Reflex 2, глубокоматовая, подготовка Q3	Tikkurila F497 «Paper»	17,5 м²
О9	стены	окраска, Tikkurila Joker, шелковисто-матовая, подготовка К3	Tikkurila F497 «Paper»	20,2 м²

Допущения и предложения на листе

Основа листа: размеры сняты с размерных цепочек растрового скана плана заказчика, на объекте не замерены; ступени наружного контура приведены к граням помещений модели (ИЗ-8, К-20, К-21); высота потолка 2700 мм принята, источника нет (К-24); тип дома и перекрытие (монолит, плита 220 мм) приняты, источника нет (К-3); толщины стен приняты (250 и 120 мм), источника нет (К-21); мощность 15 кВт принята, технических условий нет (К-25).

См. лист открытых вопросов (лист 6, запись К-3; лист 7, записи К-20, К-21, К-24, К-25; лист 10, запись ИЗ-8).

Примечания

1. Развёртки — вид на стену изнутри помещения, по часовой стрелке; расположение — на схеме листа и на листе 90; размеры — в мм по чистовым поверхностям; отметки — в м от ±0,000; высоты Н — от чистого пола помещения до оси изделия, у декора — до центра.
2. Красные цепочки — привязки электроточек и выводов: по горизонтали от угла чистовых стен, по вертикали от чистого пола, до оси изделия; звенья короче 3 мм на листе вынесены во второй ярус (ближняя к стене цепочка).
3. У знака электроточки: марка (Р — розетка, S — выключатель, Св — светильник, ЭВ — вывод кабеля), ×N — число постов в рамке, гр. — группа щита, Н — высота оси от чистого пола, мм; группы по клавишам выключателя — на листе выключателей.
4. Схема мебели, приборов и декора не является технической документацией для производства мебели; габариты — по паспортам изделий.
5. Картины и зеркала крепить к основанию по паспорту изделия (закладные и анкеры — в перечне скрытых работ); крест — ось центра предмета.

1000 мм · печать 1:1

Изм.	Кол.уч	Лист	№ док.	Подп.	Дата
Разраб.		Кырлан А.С.			21.10.26
Пров.					
ГИП		Кырлан А.С.			21.10.26
Н. контр.					
Утв.					

ГД-2026-004-АИ

Четырёхкомнатная квартира

Общая площадь 102,67* м² · * размеры со скана, не замерены (реестр — л. 6–11, ИЗ-8, К-20, К-21)

Дизайн-проект интерьера четырёхкомнатной квартиры

Стадия	Лист	Листов
РП	99	124

Развёртки стен В, Г. Детская 1 (пом. 4)

М 1:40

Кырлан Александр Сергеевич

выпуск 05.10.2026 № 7e7a2cd217 · стр. 110 из 168

Развёртки стен А, Б. Коридор (пом. 5)

Коридор (пом. 5) · вид изнутри помещения · размеры в мм, отметки в м

ПРЕДВАРИТЕЛЬНО · не для производства работ · открыто пунктов: 30 (реестр — л. 6–11)

Развёртка стены А

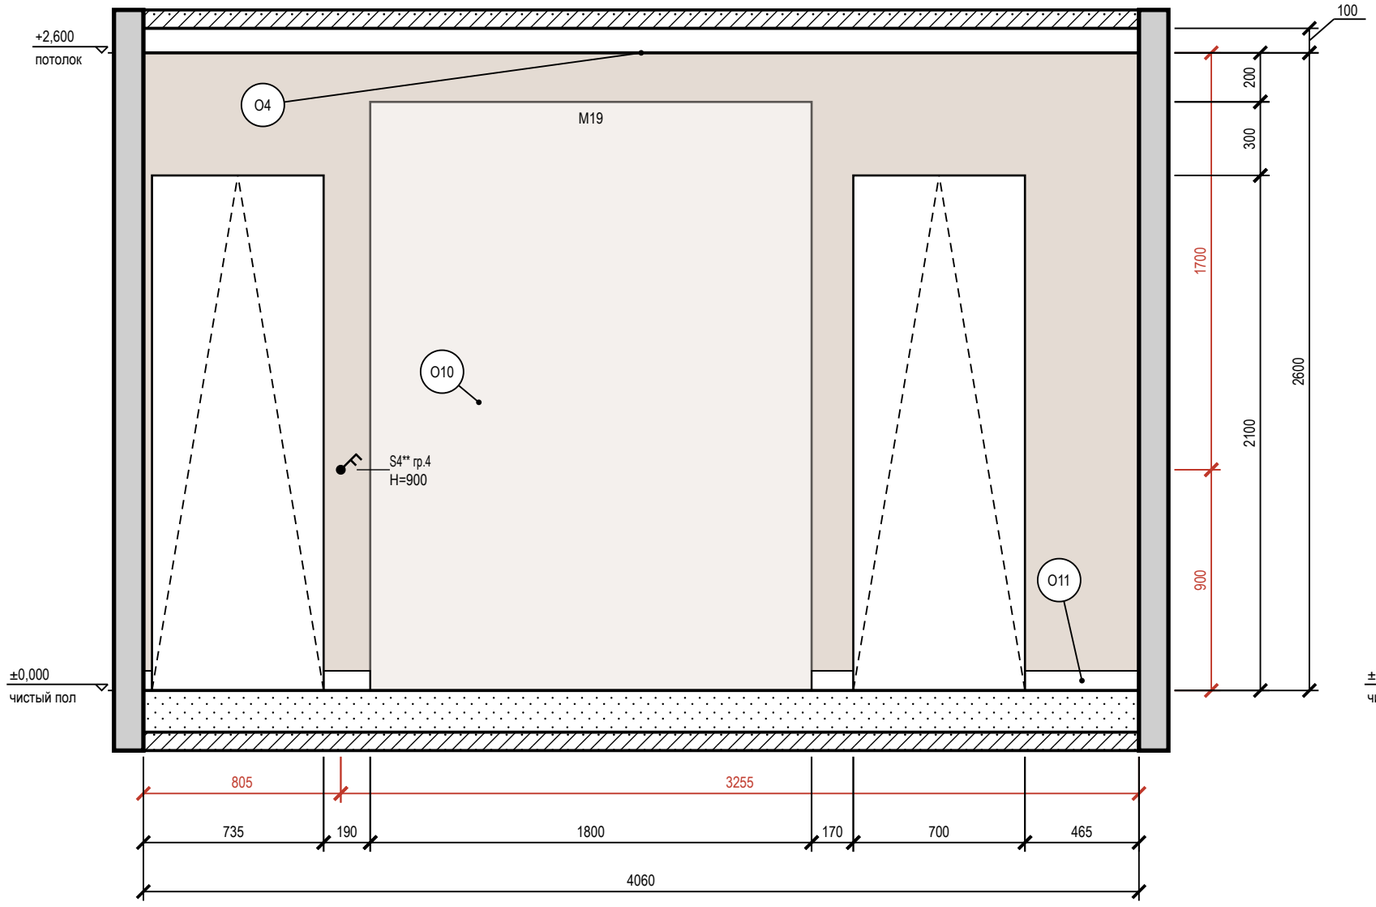

Развёртка стены Б

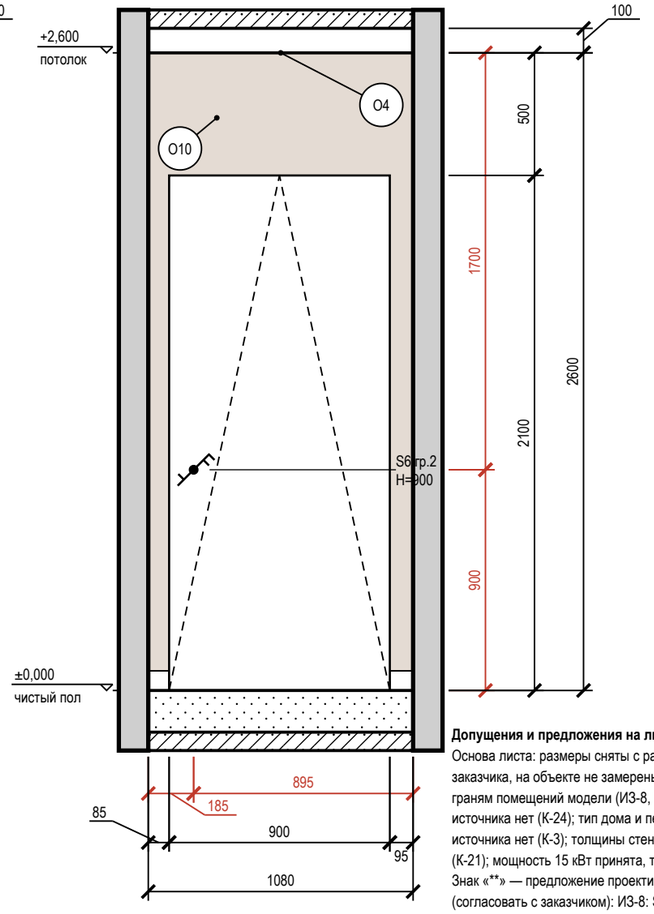

Схема развёрток (М 1:100)

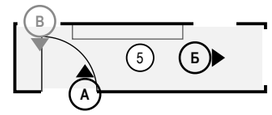

Допущения и предложения на листе

Основа листа: размеры сняты с размерных цепочек растрового скана плана заказчика, на объекте не замерены; ступени наружного контура приведены к граням помещений модели (ИЗ-8, К-20, К-21); высота потолка 2700 мм принята, источника нет (К-24); тип дома и перекрытие (монолит, плита 220 мм) приняты, источника нет (К-3); толщины стен приняты (250 и 120 мм), источника нет (К-21); мощность 15 кВт принята, технических условий нет (К-25).

Знак «**» — предложение проектировщика, заказчиком не утверждено (согласовать с заказчиком): ИЗ-8: S4.

См. лист открытых вопросов (лист 6, запись К-3; лист 7, записи К-20, К-21, К-24, К-25; лист 10, запись ИЗ-8).

Условные обозначения

- выключатель одноклавишный
- выключатель двухклавишный (флажков — по числу клавиш)
- выключатель с проходной или перекрёстной клавишей (обратный флажок); тип клавиши — в подписи
- привязки точек и выводов от угла и от пола, мм
- мебель и приборы — фасад по расстановке (условно)
- дверной проём; марка двери — в кружке
- стены и перекрытия в сечении
- окраска: тон — цвет по коду производителя (условно)
- О1 — марка отделки по реестру отделки альбома
- А — марка развёртки: буква стены, стрелка — взгляд

Ведомость отделки (на листе)

Марка	Поверхность	Материал, изделие	Цвет, код	Кол.
О4	потолок	окраска, Tikkurila Anti-Reflex 2, глубокоматовая, подготовка Q3	Tikkurila F497 «Paper»	4,5 м²
О10	стены	окраска, Tikkurila Optiva 20 Semimatt, шелковисто-матовая, подготовка К3	Tikkurila J484 «Castle»	8,5 м²
О11	плинтус	плинтус МДФ, h 80 мм, аналог: плинтус МДФ под окраску 80×16 мм, полуглянцевая	Tikkurila J484 «Castle»	1 м

Примечания

1. Развёртки — вид на стену изнутри помещения, по часовой стрелке; расположение — на схеме листа и на листе 90; размеры — в мм по чистовым поверхностям; отметки — в м от ±0,000; высоты Н — от чистого пола помещения до оси изделия, у декора — до центра.
2. Красные цепочки — привязки электроточек и выводов: по горизонтали от угла чистовых стен, по вертикали от чистого пола, до оси изделия; звенья короче 3 мм на листе вынесены во второй ярус (ближняя к стене цепочка).
3. У знака электроточки: марка (Р — розетка, S — выключатель, Св — светильник, ЭВ — вывод кабеля), ×N — число постов в рамке, гр. — группа щита, Н — высота оси от чистого пола, мм; группы по клавишам выключателя — на листе выключателей.
4. Схема мебели, приборов и декора не является технической документацией для производства мебели; габариты — по паспортам изделий.

1000 мм · печать 1:1

Изм.	Кол.уч	Лист	№ док.	Подп.	Дата
Разраб.		Кырлан А.С.			21.10.26
Пров.					
ГИП		Кырлан А.С.			21.10.26
Н. контр.					
Утв.					

ГД-2026-004-АИ

Четырёхкомнатная квартира

Общая площадь 102,67* м² · * размеры со скана, не замерены (реестр — л. 6–11, ИЗ-8, К-20, К-21)

Дизайн-проект интерьера четырёхкомнатной квартиры

Стадия	Лист	Листов
РП	100	124

Развёртки стен А, Б. Коридор (пом. 5)

М 1:25

Кырлан Александр Сергеевич

выпуск 05.10.2026 № 7e7a2cd217 · стр. 111 из 168

Развёртка стены В. Коридор (пом. 5)

Коридор (пом. 5) · вид изнутри помещения · размеры в мм, отметки в м

ПРЕДВАРИТЕЛЬНО · не для производства работ · открыто пунктов: 30 (реестр — л. 6–11)

Развёртка стены В

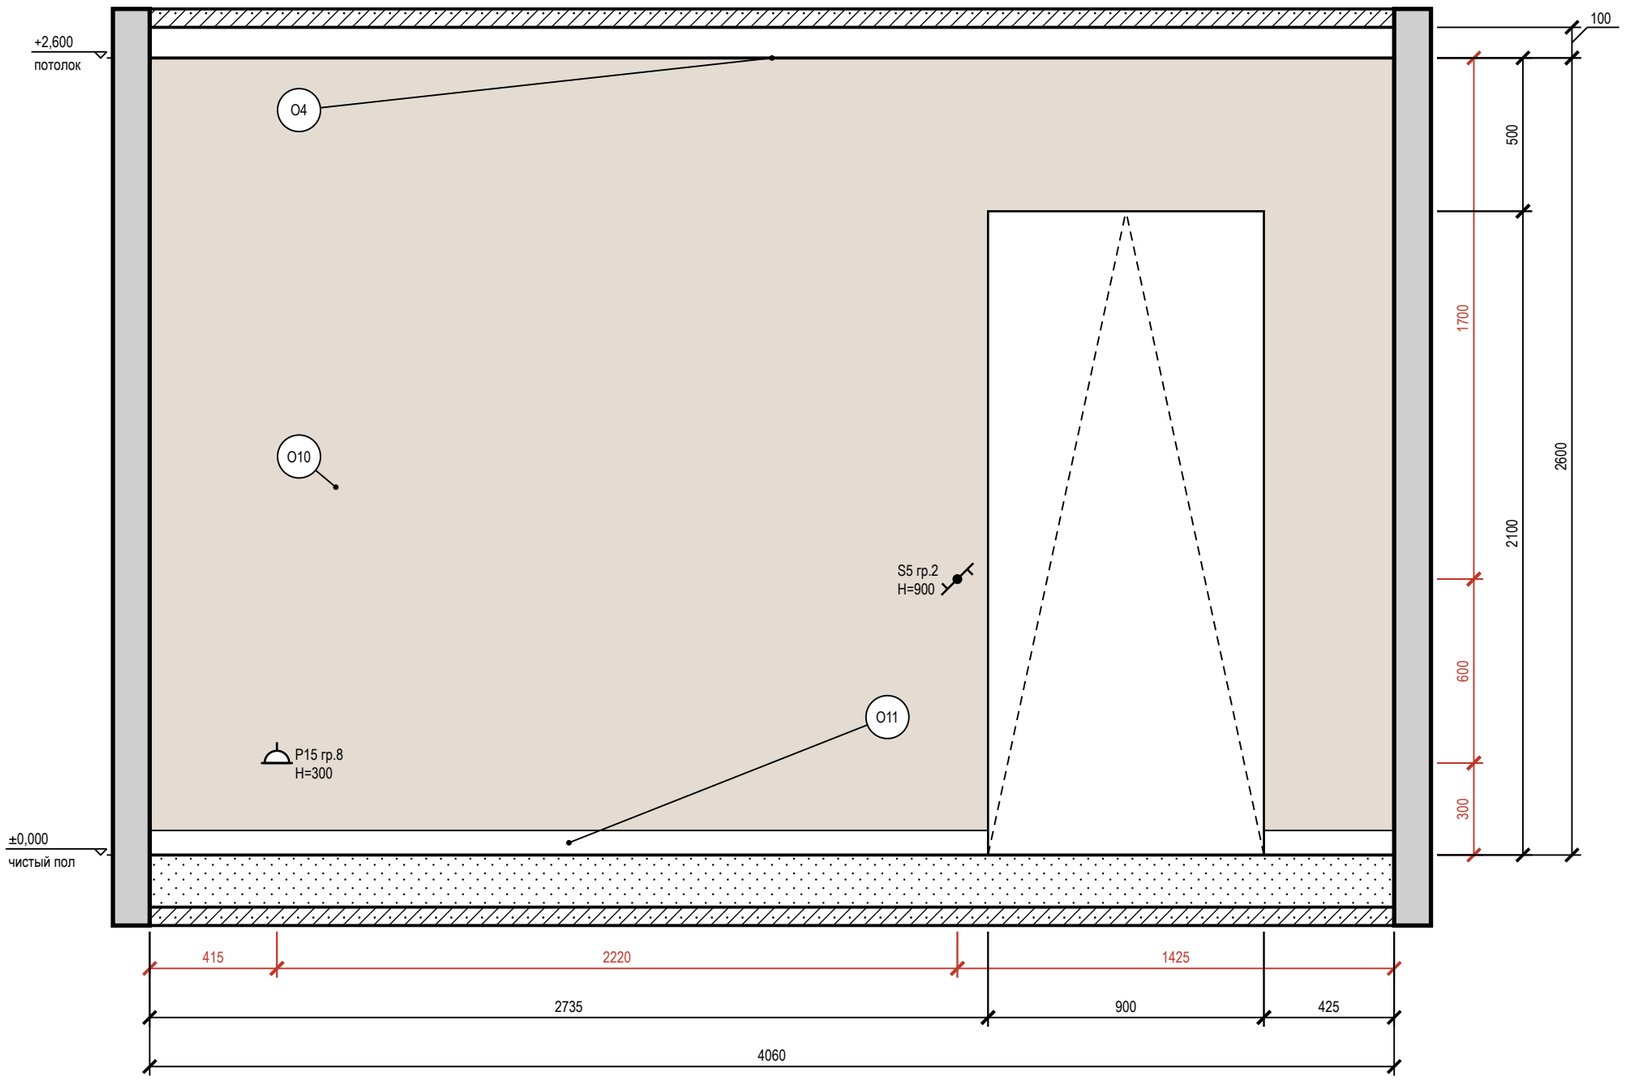

Схема развёрток (М 1:100)

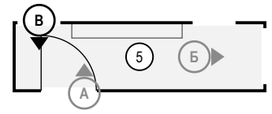

Условные обозначения

- розетка с заземляющим контактом; у знака — марка, ×N постов в рамке, гр. — группа щита, Н — высота оси, мм
- выключатель одноклавишный
- выключатель с проходной или перекрёстной клавишей (обратный флажок); тип клавиши — в подписи
- привязки точек и выводов от угла и от пола, мм
- мебель и приборы — фасад по расстановке (условно)
- дверной проём; марка двери — в кружке
- стены и перекрытия в сечении
- окраска: тон — цвет по коду производителя (условно)
- О1 — марка отделки по реестру отделки альбома
- А — марка развёртки: буква стены, стрелка — взгляд

Ведомость отделки (на листе)

Марка	Поверхность	Материал, изделие	Цвет, код	Кол.
О4	потолок	окраска, Tikkurila Anti-Reflex 2, глубокоматовая, подготовка Q3	Tikkurila F497 «Paper»	4,5 м²
О10	стены	окраска, Tikkurila Optiva 20 Semimatt, шелковисто-матовая, подготовка К3	Tikkurila J484 «Castle»	8,7 м²
О11	плинтус	плинтус МДФ, h 80 мм, аналог: плинтус МДФ под окраску 80×16 мм, полуглянцевая	Tikkurila J484 «Castle»	3,2 м

Допущения и предложения на листе

Основа листа: размеры сняты с размерных цепочек растрового скана плана заказчика, на объекте не замерены; ступени наружного контура приведены к граням помещений модели (ИЗ-8, К-20, К-21); высота потолка 2700 мм принята, источника нет (К-24); тип дома и перекрытие (монолит, плита 220 мм) приняты, источника нет (К-3); толщины стен приняты (250 и 120 мм), источника нет (К-21); мощность 15 кВт принята, технических условий нет (К-25).

См. лист открытых вопросов (лист 6, запись К-3; лист 7, записи К-20, К-21, К-24, К-25; лист 10, запись ИЗ-8).

Примечания

1. Развёртки — вид на стену изнутри помещения, по часовой стрелке; расположение — на схеме листа и на листе 90; размеры — в мм по чистовым поверхностям; отметки — в м от ±0,000; высоты Н — от чистого пола помещения до оси изделия, у декора — до центра.
2. Красные цепочки — привязки электроточек и выводов: по горизонтали от угла чистовых стен, по вертикали от чистого пола, до оси изделия; звенья короче 3 мм на листе вынесены во второй ярус (ближняя к стене цепочка).
3. У знака электроточки: марка (Р — розетка, S — выключатель, Св — светильник, ЭВ — вывод кабеля), ×N — число постов в рамке, гр. — группа щита, Н — высота оси от чистого пола, мм; группы по клавишам выключателя — на листе выключателей.
4. Схема мебели, приборов и декора не является технической документацией для производства мебели; габариты — по паспортам изделий.

1000 мм · печать 1:1

Изм.	Кол.уч	Лист	№ док.	Подп.	Дата
Разраб.		Кырлан А.С.			21.10.26
Пров.					
ГИП		Кырлан А.С.			21.10.26
Н. контр.					
Утв.					

ГД-2026-004-АИ

Четырёхкомнатная квартира

Общая площадь 102,67* м² · * размеры со скана, не замерены (реестр — л. 6–11, ИЗ-8, К-20, К-21)

Дизайн-проект интерьера четырёхкомнатной квартиры

Стадия	Лист	Листов
РП	101	124

Развёртка стены В. Коридор (пом. 5)

М 1:20

Кырлан Александр Сергеевич

выпуск 05.10.2026 № 7e7a2cd217 · стр. 112 из 168

Развёртка стены А. Кухня (пом. 6), кухонный фронт

Кухня (пом. 6) · вид изнутри помещения · размеры в мм, отметки в м

ПРЕДВАРИТЕЛЬНО · не для производства работ · открыто пунктов: 30 (реестр — л. 6–11)

Развёртка стены А

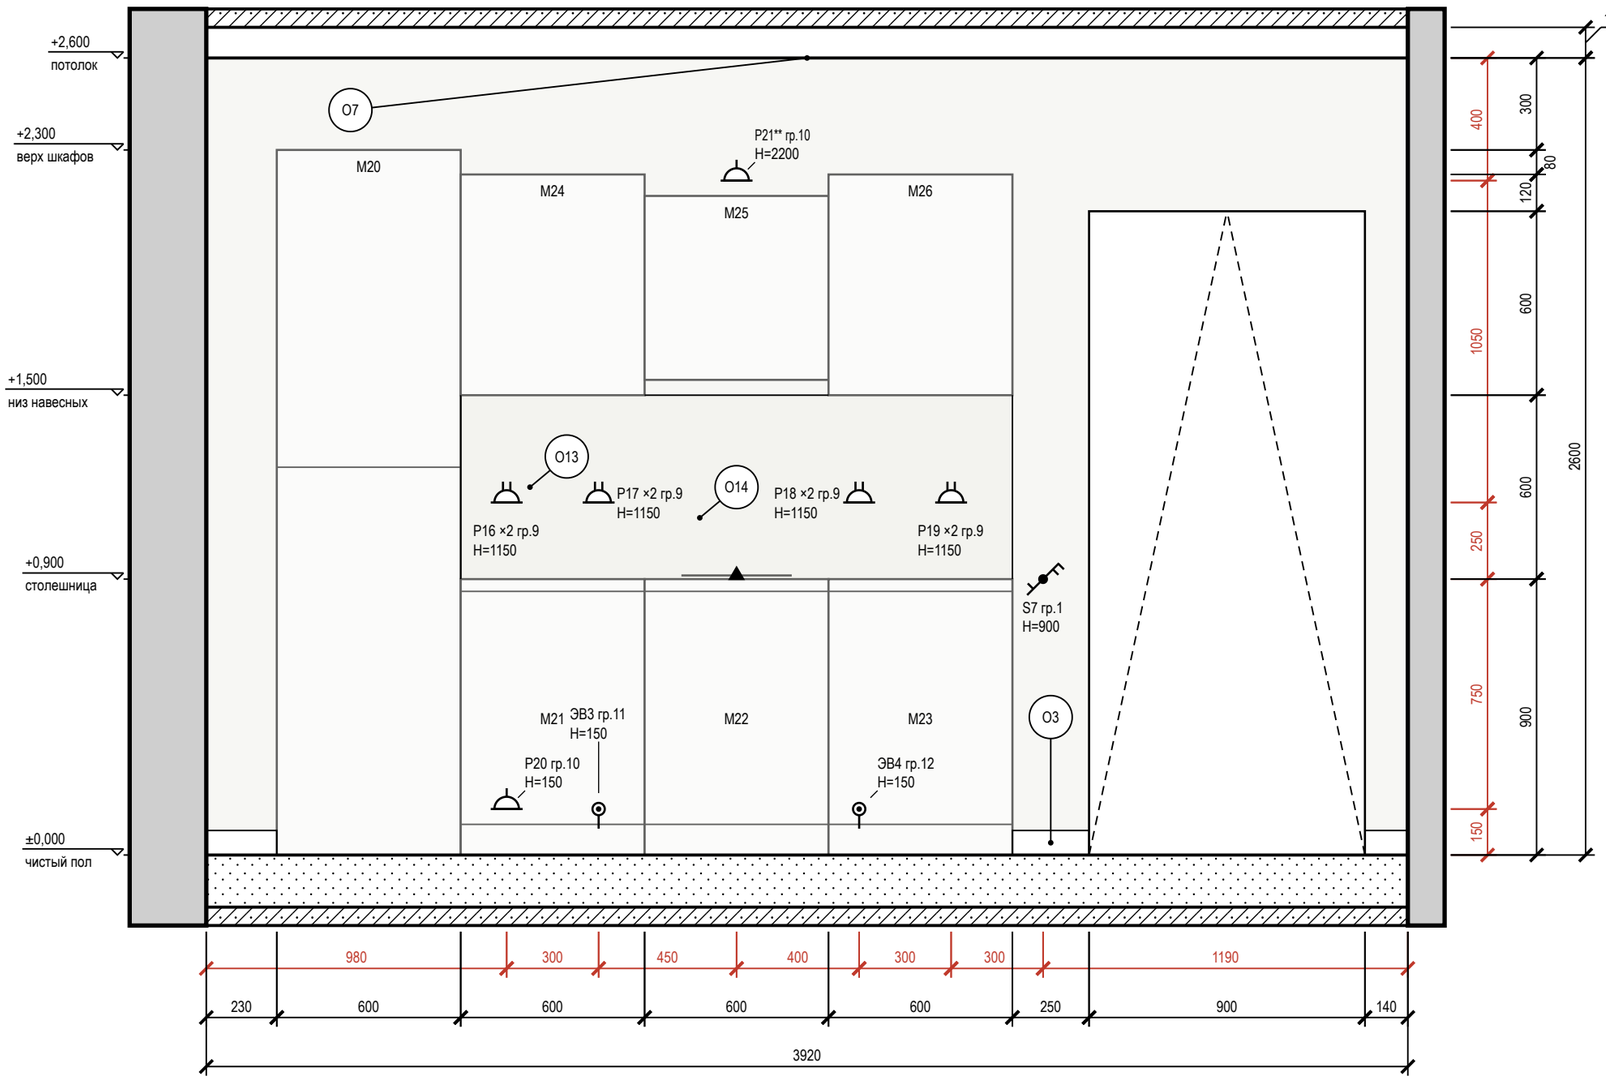

Схема развёрток (М 1:100)

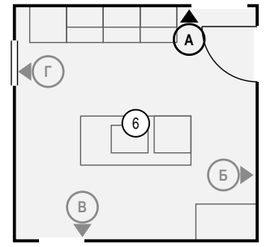

Условные обозначения

- розетка с заземляющим контактом; у знака — марка, ×N постов в рамке, гр. — группа щита, Н — высота оси, мм
- вывод кабеля для подключения прибора (без розетки), марка ЭВ
- выключатель одноклавишный
- выключатель двухклавишный (флажков — по числу клавиш)
- выключатель с проходной или перекрёстной клавишей (обратный флажок); тип клавиши — в подписи
- привязки точек и выводов от угла и от пола, мм
- мебель и приборы — фасад по расстановке (условно)
- дверной проём; марка двери — в кружке
- стены и перекрытия в сечении
- плитка: сетка швов по формату, ▲ — ось старта
- окраска: тон — цвет по коду производителя (условно)
- О1 — марка отделки по реестру отделки альбома
- А — марка развёртки: буква стены, стрелка — взгляд

Допущения и предложения на листе

Основа листа: размеры сняты с размерных цепочек растрового скана плана заказчика, на объекте не замерены; ступени наружного контура приведены к граням помещений модели (ИЗ-8, К-20, К-21); высота потолка 2700 мм принята, источника нет (К-24); тип дома и перекрытие (монолит, плита 220 мм) приняты, источника нет (К-3); толщины стен приняты (250 и 120 мм), источника нет (К-21); мощность 15 кВт принята, технических условий нет (К-25).

Знак «**» — предложение проектировщика, заказчиком не утверждено (согласовать с заказчиком): ИЗ-10, К-23: Р21 — высота 2200 мм выше нормы 1 м (ПУЭ 6.6.30) по назначению: питание вытяжки М25, розетка в модуле за съёмной панелью.

См. лист открытых вопросов (лист 6, запись К-3; лист 7, записи К-20, К-21, К-23–К-25; лист 10, записи ИЗ-8, ИЗ-10).

Примечания

1. Развёртки — вид на стену изнутри помещения, по часовой стрелке; расположение — на схеме листа и на листе 90; размеры — в мм по чистовым поверхностям; отметки — в м от ±0,000; высоты Н — от чистого пола помещения до оси изделия, у декора — до центра.
2. Красные цепочки — привязки электроточек и выводов: по горизонтали от угла чистовых стен, по вертикали от чистого пола, до оси изделия; звенья короче 3 мм на листе вынесены во второй ярус (ближняя к стене цепочка).
3. У знака электроточки: марка (Р — розетка, S — выключатель, Св — светильник, ЭВ — вывод кабеля), ×N — число постов в рамке, гр. — группа щита, Н — высота оси от чистого пола, мм; группы по клавишам выключателя — на листе выключателей.
4. Схема мебели, приборов и декора не является технической документацией для производства мебели; габариты — по паспортам изделий.

1000 мм · печать 1:1

Изм.	Кол.уч	Лист	№ док.	Подп.	Дата
Разраб.		Кырлан А.С.			21.10.26
Пров.					
ГИП		Кырлан А.С.			21.10.26
Н. контр.					
Утв.					

ГД-2026-004-АИ

Четырёхкомнатная квартира

Общая площадь 102,67* м² · * размеры со скана, не замерены (реестр — л. 6–11, ИЗ-8, К-20, К-21)

Дизайн-проект интерьера четырёхкомнатной квартиры

Стадия	Лист	Листов
РП	102	124

Развёртка стены А. Кухня (пом. 6), кухонный фронт

М 1:20

Кырлан Александр Сергеевич

выпуск 05.10.2026 № 7e7a2cd217 · стр. 113 из 168

Развёртки стен Б, В. Кухня (пом. 6)

Кухня (пом. 6) · вид изнутри помещения · размеры в мм, отметки в м

ПРЕДВАРИТЕЛЬНО · не для производства работ · открыто пунктов: 30 (реестр — л. 6–11)

Развёртка стены Б

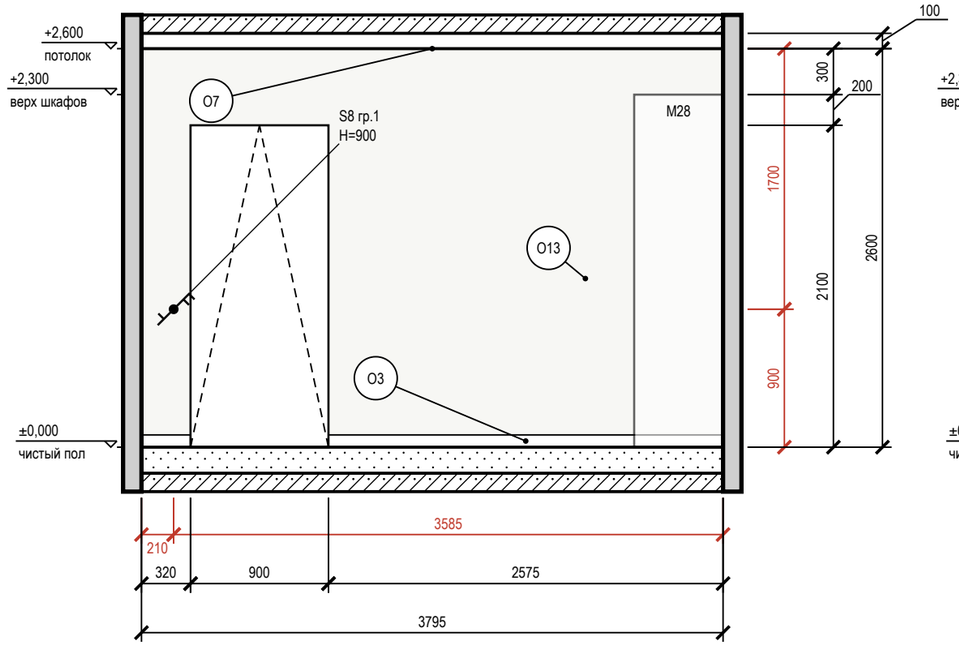

Развёртка стены В

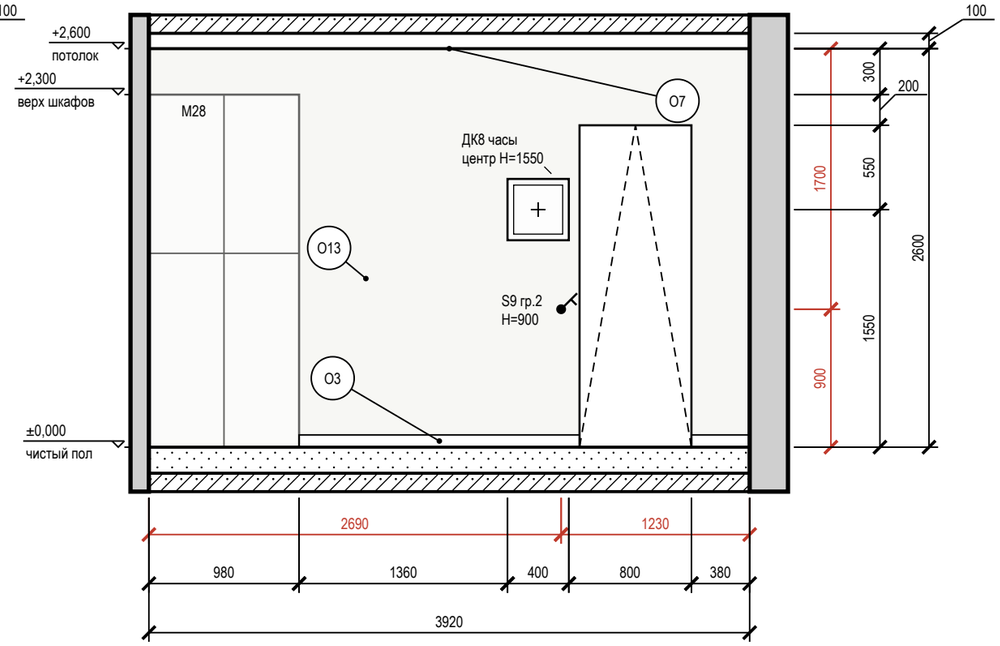

Схема развёрток (М 1:100)

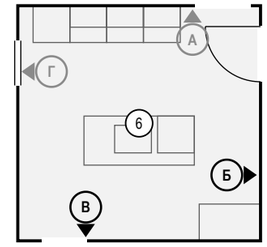

Условные обозначения

- выключатель одноклавишный
- выключатель двухклавишный (флажков — по числу клавиш)
- выключатель с проходной или перекрёстной клавишей (обратный флажок); тип клавиши — в подписи
- привязки точек и выводов от угла и от пола, мм
- мебель и приборы — фасад по расстановке (условно)
- картина (декор): марка Д, крест — центр, Н — высота центра, мм
- дверной проём; марка двери — в кружке
- стены и перекрытия в сечении
- окраска: тон — цвет по коду производителя (условно)
- О1 — марка отделки по реестру отделки альбома
- А — марка развёртки: буква стены, стрелка — взгляд

Ведомость отделки (на листе)

Марка	Поверхность	Материал, изделие	Цвет, код	Кол.
О3	плинтус	плинтус МДФ, h 80 мм, аналог: плинтус МДФ под окраску 80×16 мм, полуглянцевая	Tikkurila F497 «Paper»	5,1 м
О7	потолок	окраска, Tikkurila Luja 7, матовая, подготовка Q3	Tikkurila F497 «Paper»	15,2 м²
О13	стены	окраска, Tikkurila Luja 7, шелковисто-матовая, подготовка К3	Tikkurila F497 «Paper»	16,6 м²

Допущения и предложения на листе

Основа листа: размеры сняты с размерных цепочек растрового скана плана заказчика, на объекте не замерены; ступени наружного контура приведены к граням помещений модели (ИЗ-8, К-20, К-21); высота потолка 2700 мм принята, источника нет (К-24); тип дома и перекрытие (монолит, плита 220 мм) приняты, источника нет (К-3); толщины стен приняты (250 и 120 мм), источника нет (К-21); мощность 15 кВт принята, технических условий нет (К-25).

См. лист открытых вопросов (лист 6, запись К-3; лист 7, записи К-20, К-21, К-24, К-25; лист 10, запись ИЗ-8).

Примечания

1. Развёртки — вид на стену изнутри помещения, по часовой стрелке; расположение — на схеме листа и на листе 90; размеры — в мм по чистовым поверхностям; отметки — в м от ±0,000; высоты Н — от чистого пола помещения до оси изделия, у декора — до центра.
2. Красные цепочки — привязки электроточек и выводов: по горизонтали от угла чистовых стен, по вертикали от чистого пола, до оси изделия; звенья короче 3 мм на листе вынесены во второй ярус (ближняя к стене цепочка).
3. У знака электроточки: марка (Р — розетка, S — выключатель, Св — светильник, ЭВ — вывод кабеля), ×N — число постов в рамке, гр. — группа щита, Н — высота оси от чистого пола, мм; группы по клавишам выключателя — на листе выключателей.
4. Схема мебели, приборов и декора не является технической документацией для производства мебели; габариты — по паспортам изделий.
5. Картины и зеркала крепить к основанию по паспорту изделия (закладные и анкеры — в перечне скрытых работ); крест — ось центра предмета.

1000 мм · печать 1:1

Изм.	Кол.уч	Лист	№ док.	Подп.	Дата
Разраб.		Кырлан А.С.			21.10.26
Пров.					
ГИП		Кырлан А.С.			21.10.26
Н. контр.					
Утв.					

ГД-2026-004-АИ

Четырёхкомнатная квартира

Общая площадь 102,67* м² · * размеры со скана, не замерены (реестр — л. 6–11, ИЗ-8, К-20, К-21)

Дизайн-проект интерьера четырёхкомнатной квартиры

Стадия	Лист	Листов
РП	103	124

Развёртки стен Б, В. Кухня (пом. 6)

М 1:40

Кырлан Александр Сергеевич

выпуск 05.10.2026 № 7e7a2cd217 · стр. 114 из 168

Развёртка стены Г. Кухня (пом. 6)

Кухня (пом. 6) · вид изнутри помещения · размеры в мм, отметки в м

ПРЕДВАРИТЕЛЬНО · не для производства работ · открыто пунктов: 30 (реестр — л. 6–11)

Развёртка стены Г

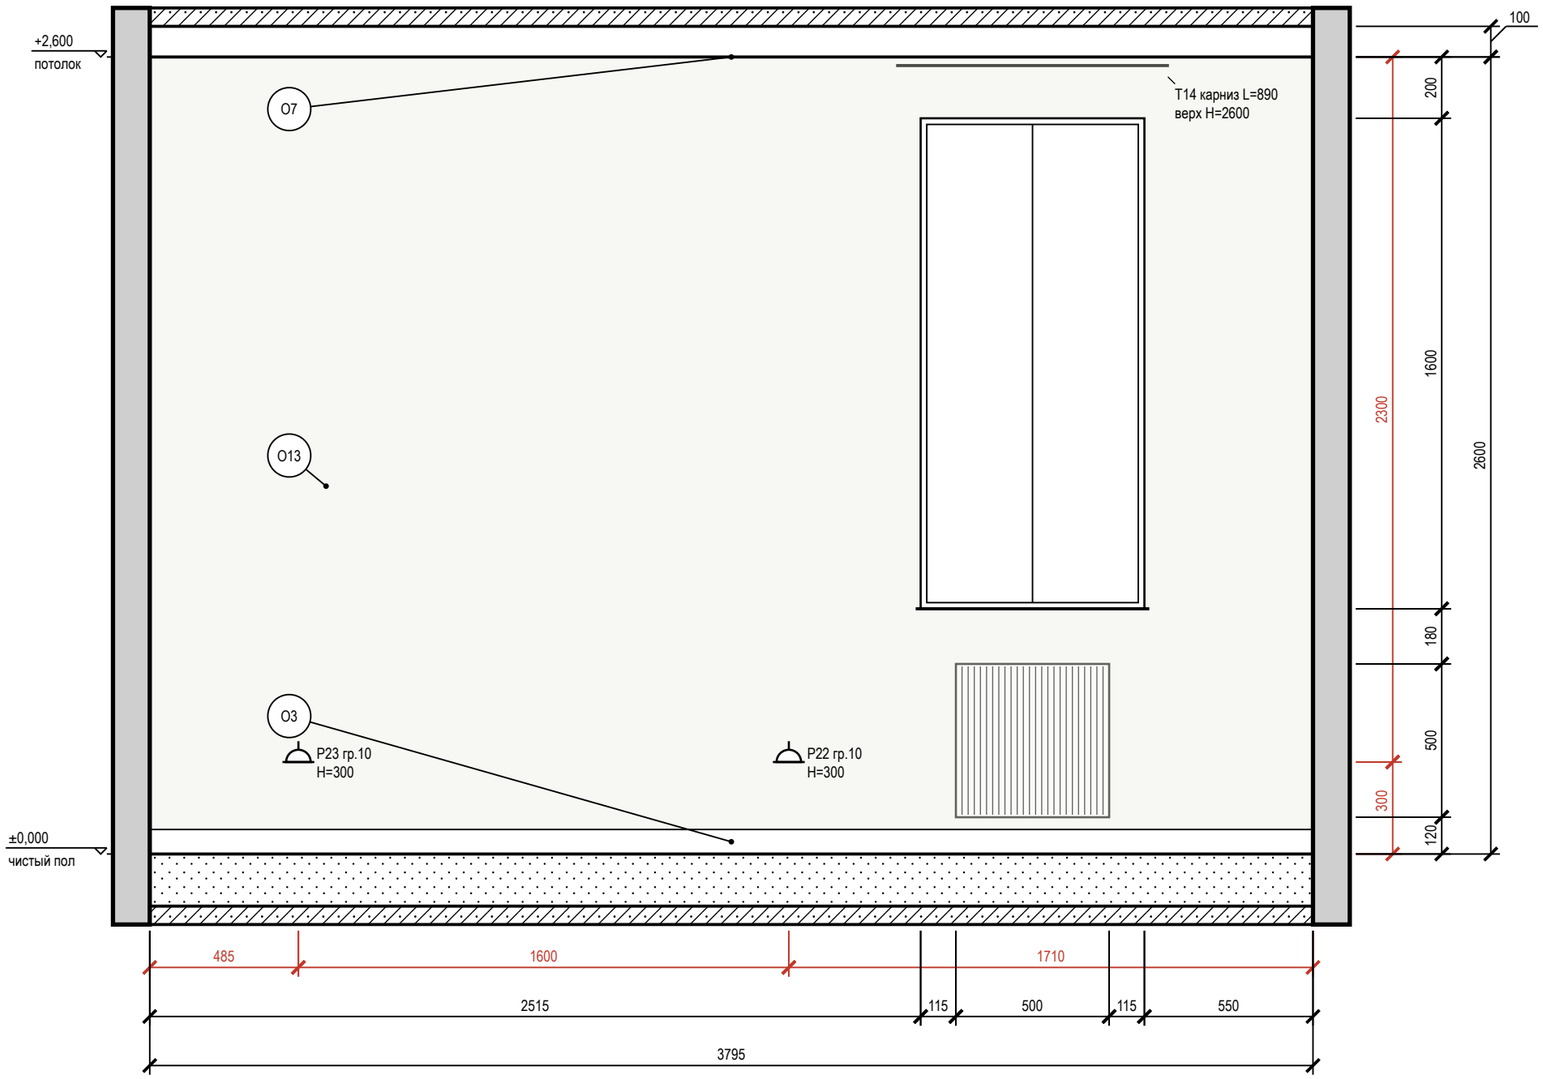

Схема развёрток (М 1:100)

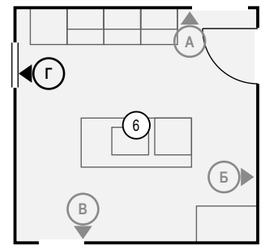

Условные обозначения

- розетка с заземляющим контактом; у знака — марка, ×N постов в рамке, гр. — группа щита, Н — высота оси, мм
- привязки точек и выводов от угла и от пола, мм
- мебель и приборы — фасад по расстановке (условно)
- карниз (шина) и шторы в собранном виде: марка Т, длина L, верх Н
- окно: проём, рама, подоконник
- радиатор отопления; марка — по плану отопления
- стены и перекрытия в сечении
- окраска: тон — цвет по коду производителя (условно)
- О1 — марка отделки по реестру отделки альбома
- А — марка развёртки: буква стены, стрелка — взгляд

Ведомость отделки (на листе)

Марка	Поверхность	Материал, изделие	Цвет, код	Кол.
О3	плинтус	плинтус МДФ, h 80 мм, аналог: плинтус МДФ под окраску 80×16 мм, полуглянцевая	Tikkurila F497 «Paper»	3,8 м
О7	потолок	окраска, Tikkurila Luja 7, матовая, подготовка Q3	Tikkurila F497 «Paper»	15,2 м²
О13	стены	окраска, Tikkurila Luja 7, шелковисто-матовая, подготовка К3	Tikkurila F497 «Paper»	8,7 м²

Допущения и предложения на листе

Основа листа: размеры сняты с размерных цепочек растрового скана плана заказчика, на объекте не замерены; ступени наружного контура приведены к граням помещений модели (ИЗ-8, К-20, К-21); высота потолка 2700 мм принята, источника нет (К-24); тип дома и перекрытие (монолит, плита 220 мм) приняты, источника нет (К-3); толщины стен приняты (250 и 120 мм), источника нет (К-21); мощность 15 кВт принята, технических условий нет (К-25).

См. лист открытых вопросов (лист 6, запись К-3; лист 7, записи К-20, К-21, К-24, К-25; лист 10, запись ИЗ-8).

Примечания

1. Развёртки — вид на стену изнутри помещения, по часовой стрелке; расположение — на схеме листа и на листе 90; размеры — в мм по чистовым поверхностям; отметки — в м от ±0,000; высоты Н — от чистого пола помещения до оси изделия, у декора — до центра.
2. Красные цепочки — привязки электроточек и выводов: по горизонтали от угла чистовых стен, по вертикали от чистого пола, до оси изделия; звенья короче 3 мм на листе вынесены во второй ярус (ближняя к стене цепочка).
3. У знака электроточки: марка (Р — розетка, S — выключатель, Св — светильник, ЭВ — вывод кабеля), ×N — число постов в рамке, гр. — группа щита, Н — высота оси от чистого пола, мм; группы по клавишам выключателя — на листе выключателей.
4. Схема мебели, приборов и декора не является технической документацией для производства мебели; габариты — по паспортам изделий.
5. Карнизы (шины) — по ведомости текстиля декоратора; длина L и верх Н — по развёртке, крепление — до окраски потолка.

1000 мм · печать 1:1

Изм.	Кол.уч	Лист	№ док.	Подп.	Дата
Разраб.		Кырлан А.С.			21.10.26
Пров.					
ГИП		Кырлан А.С.			21.10.26
Н. контр.					
Утв.					

ГД-2026-004-АИ

Четырёхкомнатная квартира

Общая площадь 102,67* м² · * размеры со скана, не замерены (реестр — л. 6–11, ИЗ-8, К-20, К-21)

Дизайн-проект интерьера четырёхкомнатной квартиры

Стадия	Лист	Листов
РП	104	124

Развёртка стены Г. Кухня (пом. 6)

М 1:20

Кырлан Александр Сергеевич

выпуск 05.10.2026 № 7e7a2cd217 · стр. 115 из 168

Развёртки стен А, Б, В. Прихожая-коридор (пом. 7)

Прихожая-коридор (пом. 7) · вид изнутри помещения · размеры в мм, отметки в м

ПРЕДВАРИТЕЛЬНО · не для производства работ · открыто пунктов: 30 (реестр — л. 6–11)

Развёртка стены А

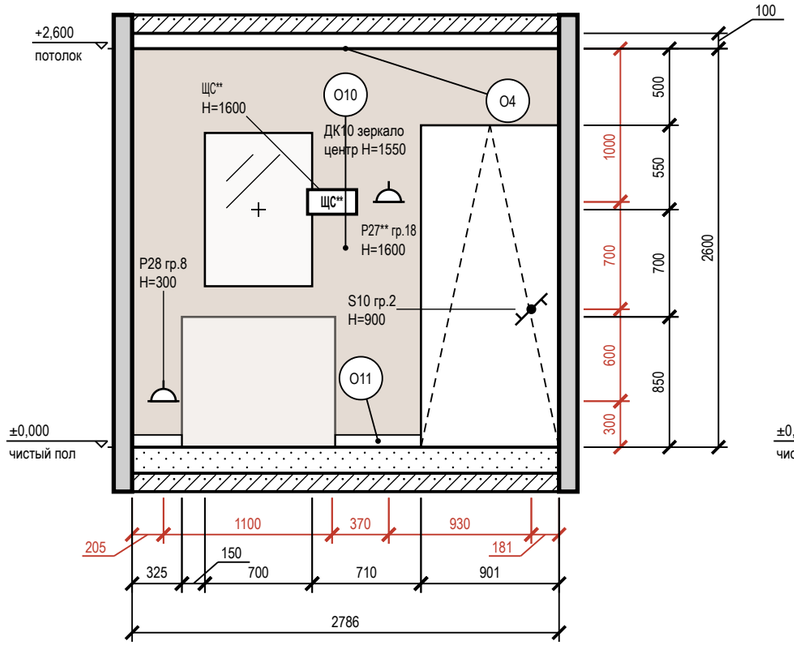

Развёртка стены Б

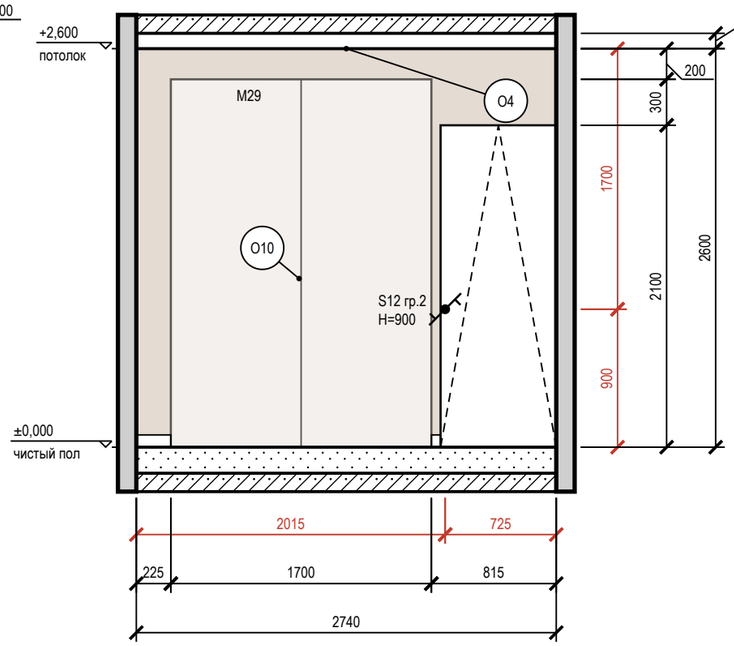

Развёртка стены В

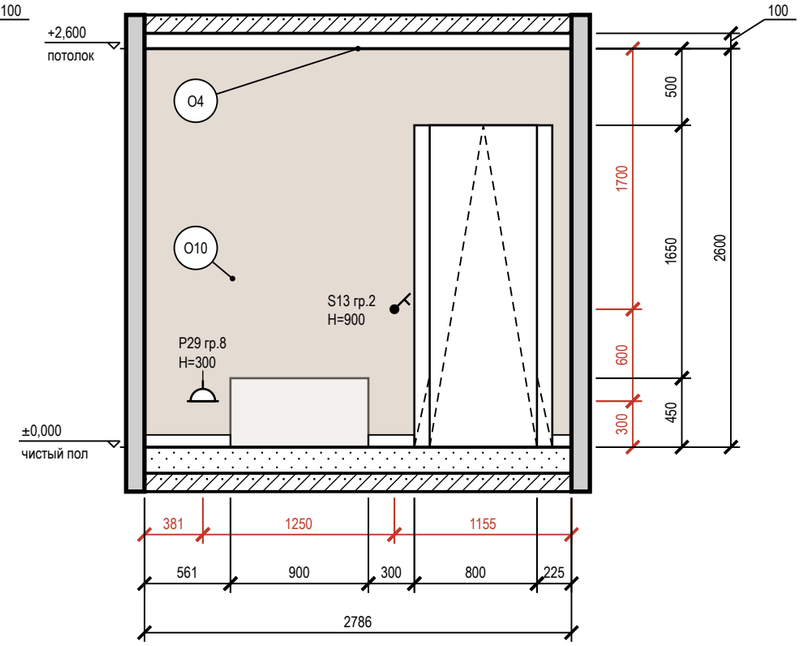

Схема развёрток (М 1:100)

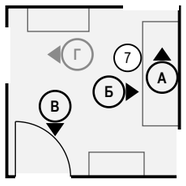

Условные обозначения

- розетка с заземляющим контактом; у знака — марка, ×N постов в рамке, гр. — группа щита, Н — высота оси, мм
- выключатель одноклавишный
- выключатель с проходной или перекрёстной клавишей (обратный флажок); тип клавиши — в подписи
- ЩК — щит квартирный
- привязки точек и выводов от угла и от пола, мм
- мебель и приборы — фасад по расстановке (условно)
- зеркало: марка Д, крест — центр, Н — высота центра, мм
- дверной проём; марка двери — в кружке
- стены и перекрытия в сечении
- окраска: тон — цвет по коду производителя (условно)
- О1 — марка отделки по реестру отделки альбома
- А — марка развёртки: буква стены, стрелка — взгляд

Ведомость отделки (на листе)

Марка	Поверхность	Материал, изделие	Цвет, код	Кол.
О4	потолок	окраска, Tikkurila Anti-Reflex 2, глубокоматовая, подготовка Q3	Tikkurila F497 «Paper»	7,8 м²
О10	стены	окраска, Tikkurila Optiva 20 Semimatt, шелковисто-матовая, подготовка К3	Tikkurila J484 «Castle»	14,8 м²
О11	плинтус	плинтус МДФ, h 80 мм, аналог: плинтус МДФ под окраску 80×16 мм, полуглянцевая	Tikkurila J484 «Castle»	2,2 м

Допущения и предложения на листе

Основа листа: размеры сняты с размерных цепочек растрового скана плана заказчика, на объекте не замерены; ступени наружного контура приведены к граням помещений модели (ИЗ-8, К-20, К-21); высота потолка 2700 мм принята, источника нет (К-24); тип дома и перекрытие (монолит, плита 220 мм) приняты, источника нет (К-3); толщины стен приняты (250 и 120 мм), источника нет (К-21); мощность 15 кВт принята, технических условий нет (К-25).

Знак «**» — предложение проектировщика, заказчиком не утверждено (согласовать с заказчиком): ИЗ-8, К-23: Р27 — высота 1600 мм выше нормы 1 м (ПУЭ 6.6.30) по назначению: питание слаботочного щита ЩС, рядом со щитом на его высоте; место сдвинуто (ИЗ-8); ИЗ-9: ЩС — щит слаботочный: место и состав.

См. лист открытых вопросов (лист 6, запись К-3; лист 7, записи К-20, К-21, К-23–К-25; лист 10, записи ИЗ-8, ИЗ-9).

Примечания

1. Развёртки — вид на стену изнутри помещения, по часовой стрелке; расположение — на схеме листа и на листе 90; размеры — в мм по чистовым поверхностям; отметки — в м от ±0,000; высоты Н — от чистого пола помещения до оси изделия, у декора — до центра.
2. Красные цепочки — привязки электроточек и выводов: по горизонтали от угла чистовых стен, по вертикали от чистого пола, до оси изделия; звенья короче 3 мм на листе вынесены во второй ярус (ближняя к стене цепочка).
3. У знака электроточки: марка (Р — розетка, S — выключатель, Св — светильник, ЭВ — вывод кабеля), ×N — число постов в рамке, гр. — группа щита, Н — высота оси от чистого пола, мм; группы по клавишам выключателя — на листе выключателей.
4. Схема мебели, приборов и декора не является технической документацией для производства мебели; габариты — по паспортам изделий.
5. Картины и зеркала крепить к основанию по паспорту изделия (закладные и анкеры — в перечне скрытых работ); крест — ось центра предмета.
6. Дверь заходит за угол помещения: на развёртке показана видимая часть проёма 770 из 900 мм — проверить привязку двери в модели.

1000 мм · печать 1:1

Изм.	Кол.уч	Лист	№ док.	Подп.	Дата
Разраб.		Кырлан А.С.			21.10.26
Пров.					
ГИП		Кырлан А.С.			21.10.26
Н. контр.					
Утв.					

ГД-2026-004-АИ

Четырёхкомнатная квартира

Общая площадь 102,67* м² · * размеры со скана, не замерены (реестр — л. 6–11, ИЗ-8, К-20, К-21)

Дизайн-проект интерьера четырёхкомнатной квартиры

Стадия	Лист	Листов
РП	105	124

Развёртки стен А, Б, В. Прихожая-коридор (пом. 7)

М 1:40

Кырлан Александр Сергеевич

выпуск 05.10.2026 № 7e7a2cd217 · стр. 116 из 168

Развёртка стены Г. Прихожая-коридор (пом. 7)

Прихожая-коридор (пом. 7) · вид изнутри помещения · размеры в мм, отметки в м

ПРЕДВАРИТЕЛЬНО · не для производства работ · открыто пунктов: 30 (реестр — л. 6–11)

Развёртка стены Г

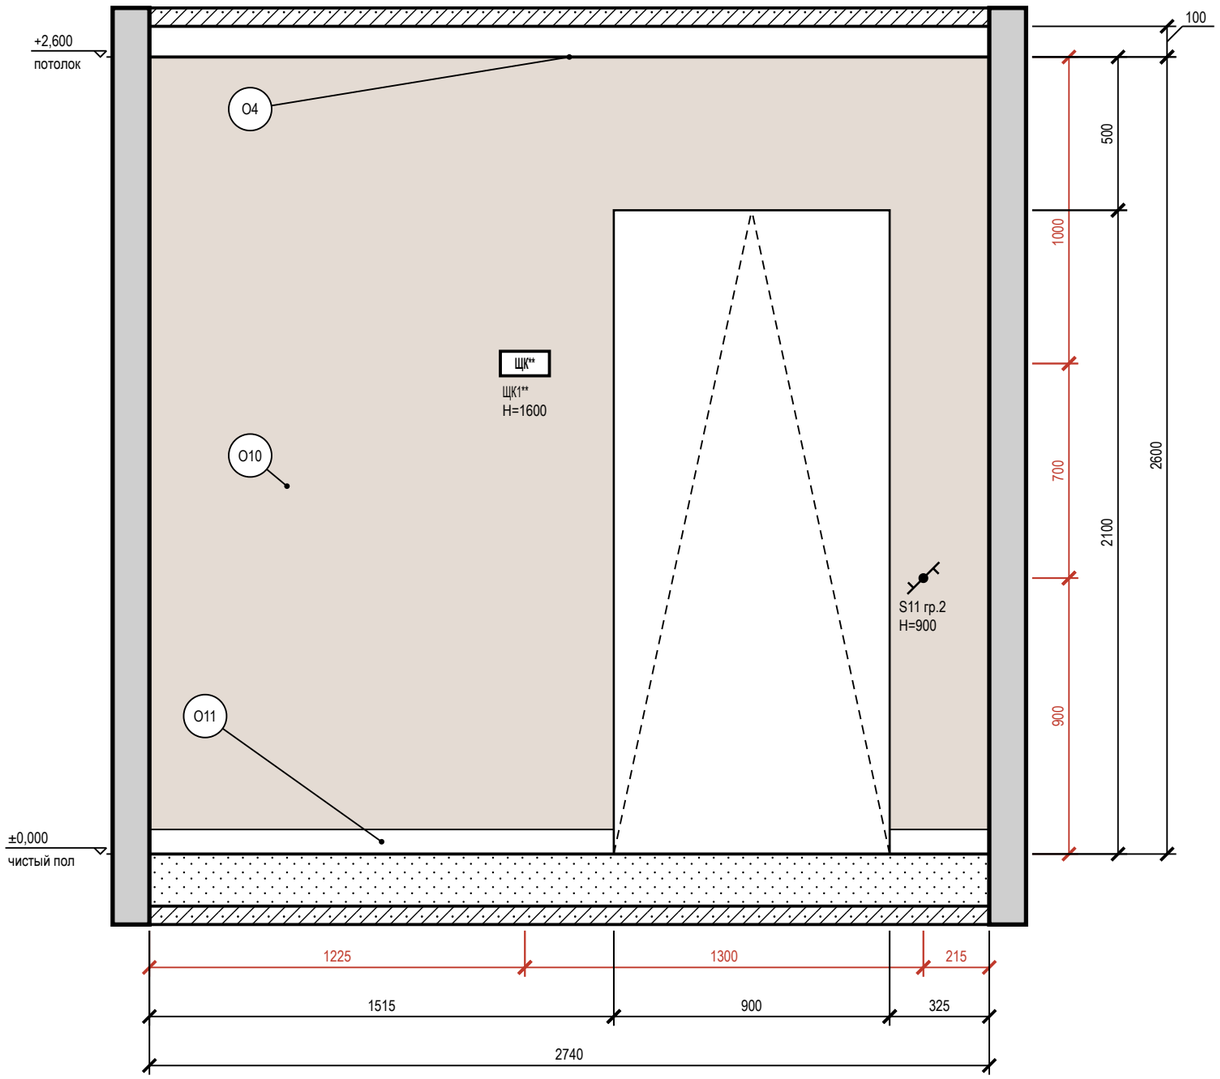

Схема развёрток (М 1:100)

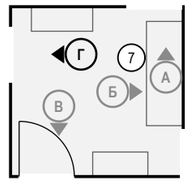

Условные обозначения

- выключатель одноклавишный
- выключатель с проходной или перекрёстной клавишей (обратный флажок); тип клавиши — в подписи
- ЩК — щит квартирный
- привязки точек и выводов от угла и от пола, мм
- мебель и приборы — фасад по расстановке (условно)
- дверной проём; марка двери — в кружке
- стены и перекрытия в сечении
- окраска: тон — цвет по коду производителя (условно)
- О1 — марка отделки по реестру отделки альбома
- А — марка развёртки: буква стены, стрелка — взгляд

Ведомость отделки (на листе)

Марка	Поверхность	Материал, изделие	Цвет, код	Кол.
О4	потолок	окраска, Tikkurila Anti-Reflex 2, глубокоматовая, подготовка Q3	Tikkurila F497 «Paper»	7,8 м²
О10	стены	окраска, Tikkurila Optiva 20 Semimatt, шелковисто-матовая, подготовка К3	Tikkurila J484 «Castle»	5,2 м²
О11	плинтус	плинтус МДФ, h 80 мм, аналог: плинтус МДФ под окраску 80×16 мм, полуглянцевая	Tikkurila J484 «Castle»	1,8 м

Допущения и предложения на листе

Основа листа: размеры сняты с размерных цепочек растрового скана плана заказчика, на объекте не замерены; ступени наружного контура приведены к граням помещений модели (ИЗ-8, К-20, К-21); высота потолка 2700 мм принята, источника нет (К-24); тип дома и перекрытие (монолит, плита 220 мм) приняты, источника нет (К-3); толщины стен приняты (250 и 120 мм), источника нет (К-21); мощность 15 кВт принята, технических условий нет (К-25).

Знак «**» — предложение проектировщика, заказчиком не утверждено (согласовать с заказчиком): ИЗ-5: ЩК1; ЩК — щит ЩРВ-П-72 вместо ЩРВ-П-54: резерв при 44 занятых модулях был меньше 20 %.

См. лист открытых вопросов (лист 6, запись К-3; лист 7, записи К-20, К-21, К-24, К-25; лист 9, запись ИЗ-5; лист 10, запись ИЗ-8).

Примечания

1. Развёртки — вид на стену изнутри помещения, по часовой стрелке; расположение — на схеме листа и на листе 90; размеры — в мм по чистовым поверхностям; отметки — в м от ±0,000; высоты H — от чистого пола помещения до оси изделия, у декора — до центра.
2. Красные цепочки — привязки электроточек и выводов: по горизонтали от угла чистовых стен, по вертикали от чистого пола, до оси изделия; звенья короче 3 мм на листе вынесены во второй ярус (ближняя к стене цепочка).
3. У знака электроточки: марка (Р — розетка, S — выключатель, Св — светильник, ЭВ — вывод кабеля), ×N — число постов в рамке, гр. — группа щита, H — высота оси от чистого пола, мм; группы по клавишам выключателя — на листе выключателей.
4. Схема мебели, приборов и декора не является технической документацией для производства мебели; габариты — по паспортам изделий.

1000 мм · печать 1:1

Изм.	Кол.уч	Лист	№ док.	Подп.	Дата
Разраб.		Кырлан А.С.			21.10.26
Пров.					
ГИП		Кырлан А.С.			21.10.26
Н. контр.					
Утв.					

ГД-2026-004-АИ

Четырёхкомнатная квартира

Общая площадь 102,67* м² · * размеры со скана, не замерены (реестр — л. 6–11, ИЗ-8, К-20, К-21)

Дизайн-проект интерьера четырёхкомнатной квартиры

Стадия	Лист	Листов
РП	106	124

Развёртка стены Г. Прихожая-коридор (пом. 7)

М 1:20

Кырлан Александр Сергеевич

выпуск 05.10.2026 № 7e7a2cd217 · стр. 117 из 168

Развёртки стен. Гардеробная 2 (пом. 8)

Гардеробная 2 (пом. 8) · вид изнутри помещения · размеры в мм, отметки в м

ПРЕДВАРИТЕЛЬНО · не для производства работ · открыто пунктов: 30 (реестр — л. 6–11)

Развёртка стены А

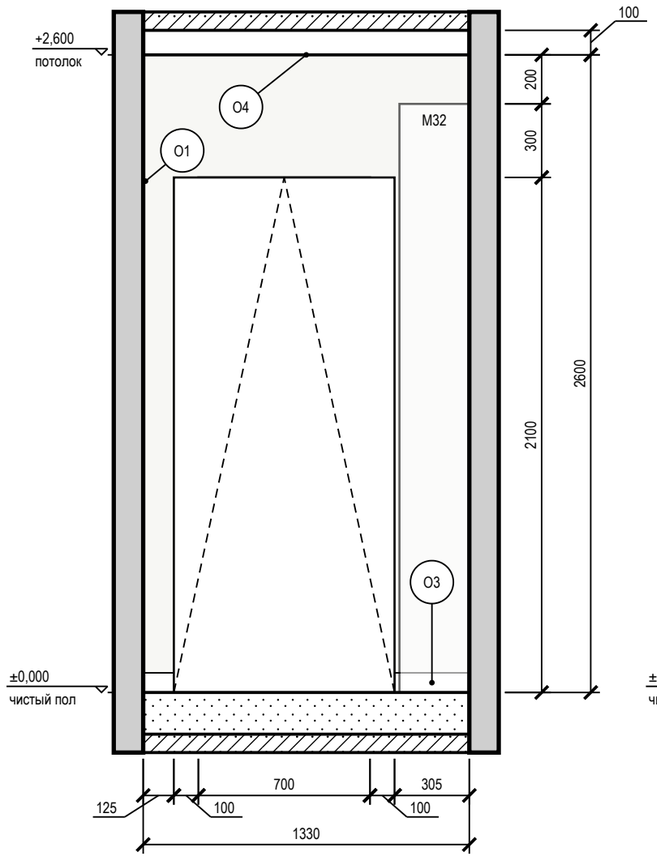

Развёртка стены Б

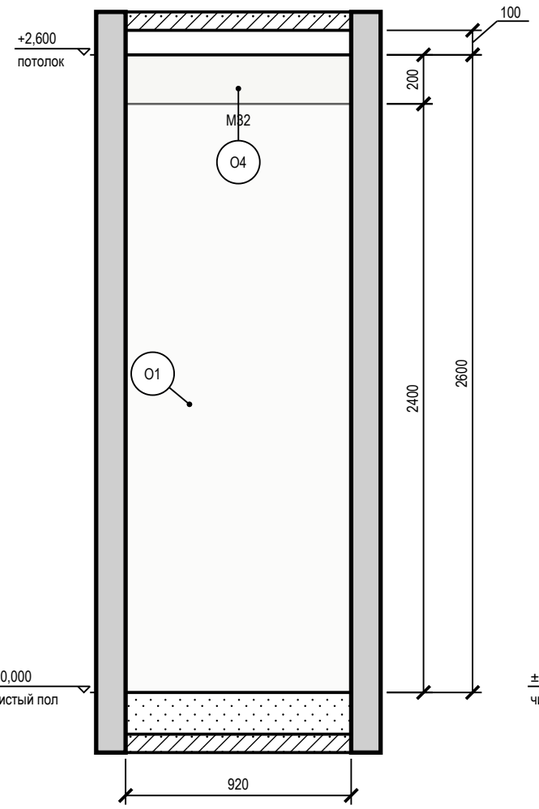

Развёртка стены В

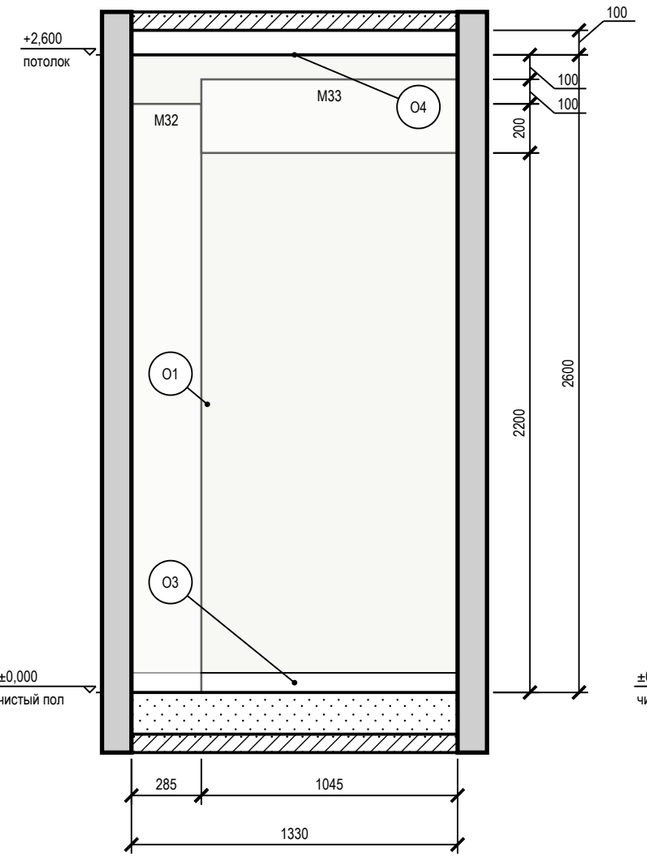

Развёртка стены Г

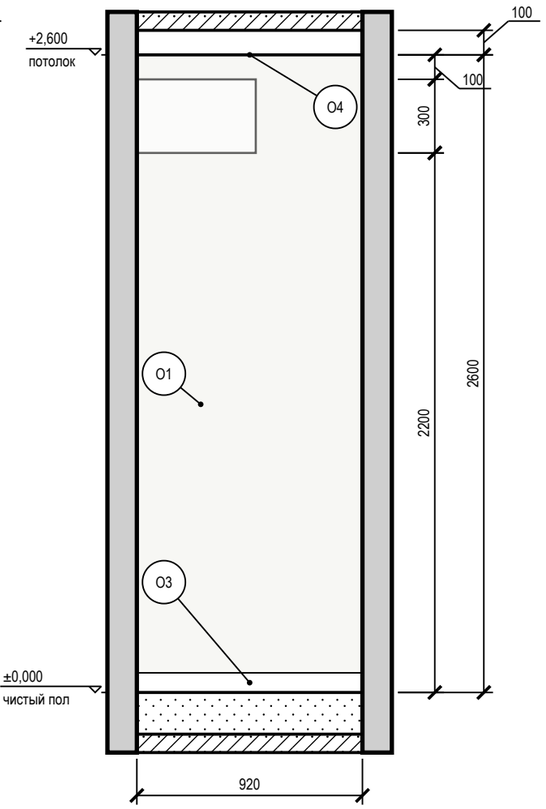

Схема развёрток (М 1:100)

Условные обозначения

- привязки точек и выводов от угла и от пола, мм
- мебель и приборы — фасад по расстановке (условно)
- дверной проём; марка двери — в кружке
- стены и перекрытия в сечении
- окраска: тон — цвет по коду производителя (условно)
- О1 — марка отделки по реестру отделки альбома
- А — марка развёртки: буква стены, стрелка — взгляд

Ведомость отделки (на листе)

Марка	Поверхность	Материал, изделие	Цвет, код	Кол.
О1	стены	окраска, Tikkurila Optiva 5 Matt, матовая, подготовка К3	Tikkurila F497 «Paper»	8,3 м²
О3	плинтус	плинтус МДФ, h 80 мм, аналог: плинтус МДФ под окраску 80×16 мм, полуглянцевая	Tikkurila F497 «Paper»	2,7 м
О4	потолок	окраска, Tikkurila Anti-Reflex 2, глубокоматовая, подготовка Q3	Tikkurila F497 «Paper»	1,3 м²

Примечания

1. Развёртки — вид на стену изнутри помещения, по часовой стрелке; расположение — на схеме листа и на листе 90; размеры — в мм по чистовым поверхностям; отметки — в м от ±0,000; высоты Н — от чистого пола помещения до оси изделия, у декора — до центра.
2. Красные цепочки — привязки электроточек и выводов: по горизонтали от угла чистовых стен, по вертикали от чистого пола, до оси изделия; звенья короче 3 мм на листе вынесены во второй ярус (ближняя к стене цепочка).
3. У знака электроточки: марка (Р — розетка, S — выключатель, Св — светильник, ЭВ — вывод кабеля), ×N — число постов в рамке, гр. — группа щита, Н — высота оси от чистого пола, мм; группы по клавишам выключателя — на листе выключателей.
4. Схема мебели, приборов и декора не является технической документацией для производства мебели; габариты — по паспортам изделий.

Допущения и предложения на листе

Основа листа: размеры сняты с размерных цепочек растрового скана плана заказчика, на объекте не замерены; ступени наружного контура приведены к граням помещений модели (ИЗ-8, К-20, К-21); высота потолка 2700 мм принята, источника нет (К-24); тип дома и перекрытие (монолит, плита 220 мм) приняты, источника нет (К-3); толщины стен приняты (250 и 120 мм), источника нет (К-21); мощность 15 кВт принята, технических условий нет (К-25).

См. лист открытых вопросов (лист 6, запись К-3; лист 7, записи К-20, К-21, К-24, К-25; лист 10, запись ИЗ-8).

1000 мм · печать 1:1

Изм.	Кол.уч	Лист	№ док.	Подп.	Дата			
Разраб.		Кырлан А.С.			21.10.26	ГД-2026-004-АИ		
Пров.						Четырёхкомнатная квартира Общая площадь 102,67* м² · * размеры со скана, не замерены (реестр — л. 6–11, ИЗ-8, К-20, К-21)		
ГИП		Кырлан А.С.			21.10.26	Дизайн-проект интерьера четырёхкомнатной квартиры	Стадия: РП	Лист: 107 / Листов: 124
Н. контр.						Развёртки стен. Гардеробная 2 (пом. 8) М 1:25	Кырлан Александр Сергеевич	
Утв.								

выпуск 05.10.2026 № 7e7a2cd217 · стр. 118 из 168

Развёртки стен А, Б. Детская 2 (пом. 9)

Детская 2 (пом. 9) · вид изнутри помещения · размеры в мм, отметки в м

ПРЕДВАРИТЕЛЬНО · не для производства работ · открыто пунктов: 30 (реестр — л. 6–11)

Развёртка стены А

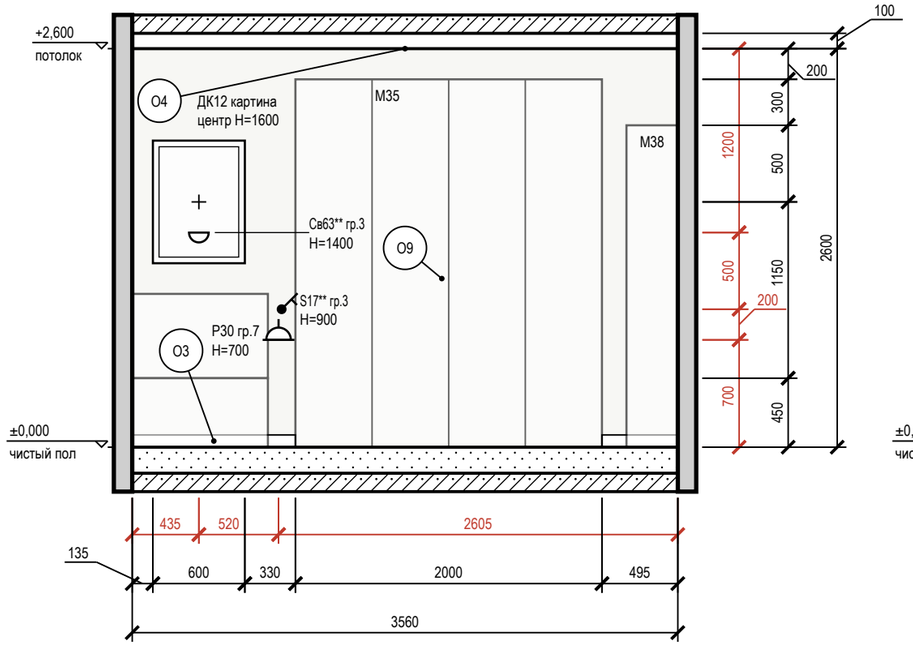

Развёртка стены Б

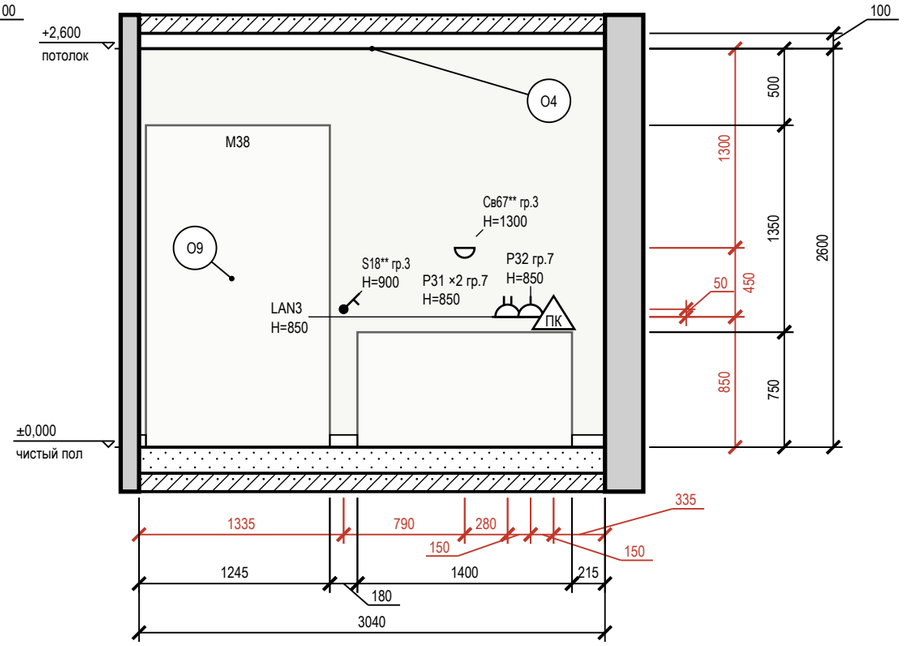

Условные обозначения

- розетка с заземляющим контактом; у знака — марка, ×N постов в рамке, гр. — группа щита, Н — высота оси, мм
- выключатель одноклавишный
- светильник настенный (бра), Н — высота оси
- ПК — розетка компьютерная RJ45
- привязки точек и выводов от угла и от пола, мм
- мебель и приборы — фасад по расстановке (условно)
- картина (декор): марка Д, крест — центр, Н — высота центра, мм
- стены и перекрытия в сечении
- окраска: тон — цвет по коду производителя (условно)
- О1 — марка отделки по реестру отделки альбома
- А — марка развёртки: буква стены, стрелка — взгляд

Схема развёрток (М 1:100)

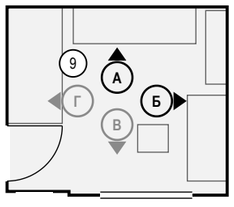

Ведомость отделки (на листе)

Марка	Поверхность	Материал, изделие	Цвет, код	Кол.
О3	плинтус	плинтус МДФ, h 80 мм, аналог: плинтус МДФ под окраску 80×16 мм, полуглянцевая	Tikkurila F497 «Paper»	2 м
О4	потолок	окраска, Tikkurila Anti-Reflex 2, глубокоматовая, подготовка Q3	Tikkurila F497 «Paper»	11 м²
О9	стены	окраска, Tikkurila Joker, шелковисто-матовая, подготовка К3	Tikkurila F497 «Paper»	17,2 м²

Допущения и предложения на листе

Основа листа: размеры сняты с размерных цепочек растрового скана плана заказчика, на объекте не замерены; ступени наружного контура приведены к граням помещений модели (ИЗ-8, К-20, К-21); высота потолка 2700 мм принята, источника нет (К-24); тип дома и перекрытие (монолит, плита 220 мм) приняты, источника нет (К-3); толщины стен приняты (250 и 120 мм), источника нет (К-21); мощность 15 кВт принята, технических условий нет (К-25).

Знак «**» — предложение проектировщика, заказчиком не утверждено (согласовать с заказчиком): ИЗ-1, К-1: окно пом. 9 (стена В); ИЗ-2: S17, Св63, S18, Св67.

См. лист открытых вопросов (лист 6, записи К-1, К-3; лист 7, записи К-20, К-21, К-24, К-25; лист 9, записи ИЗ-1, ИЗ-2; лист 10, запись ИЗ-8).

Примечания

1. Развёртки — вид на стену изнутри помещения, по часовой стрелке; расположение — на схеме листа и на листе 90; размеры — в мм по чистовым поверхностям; отметки — в м от ±0,000; высоты Н — от чистого пола помещения до оси изделия, у декора — до центра.
2. Красные цепочки — привязки электроточек и выводов: по горизонтали от угла чистовых стен, по вертикали от чистого пола, до оси изделия; звенья короче 3 мм на листе вынесены во второй ярус (ближняя к стене цепочка).
3. У знака электроточки: марка (Р — розетка, S — выключатель, Св — светильник, ЭВ — вывод кабеля), ×N — число постов в рамке, гр. — группа щита, Н — высота оси от чистого пола, мм; группы по клавишам выключателя — на листе выключателей.
4. Схема мебели, приборов и декора не является технической документацией для производства мебели; габариты — по паспортам изделий.
5. Картины и зеркала крепить к основанию по паспорту изделия (закладные и анкеры — в перечне скрытых работ); крест — ось центра предмета.

1000 мм · печать 1:1

Изм.	Кол.уч	Лист	№ док.	Подп.	Дата
Разраб.		Кырлан А.С.			21.10.26
Пров.					
ГИП		Кырлан А.С.			21.10.26
Н. контр.					
Утв.					

ГД-2026-004-АИ

Четырёхкомнатная квартира

Общая площадь 102,67* м² · * размеры со скана, не замерены (реестр — л. 6–11, ИЗ-8, К-20, К-21)

Дизайн-проект интерьера четырёхкомнатной квартиры

Стадия	Лист	Листов
РП	108	124

Развёртки стен А, Б. Детская 2 (пом. 9)

М 1:40

Кырлан Александр Сергеевич

выпуск 05.10.2026 № 7e7a2cd217 · стр. 119 из 168

Развёртки стен В, Г. Детская 2 (пом. 9)

Детская 2 (пом. 9) · вид изнутри помещения · размеры в мм, отметки в м

ПРЕДВАРИТЕЛЬНО · не для производства работ · открыто пунктов: 30 (реестр — л. 6–11)

Развёртка стены В

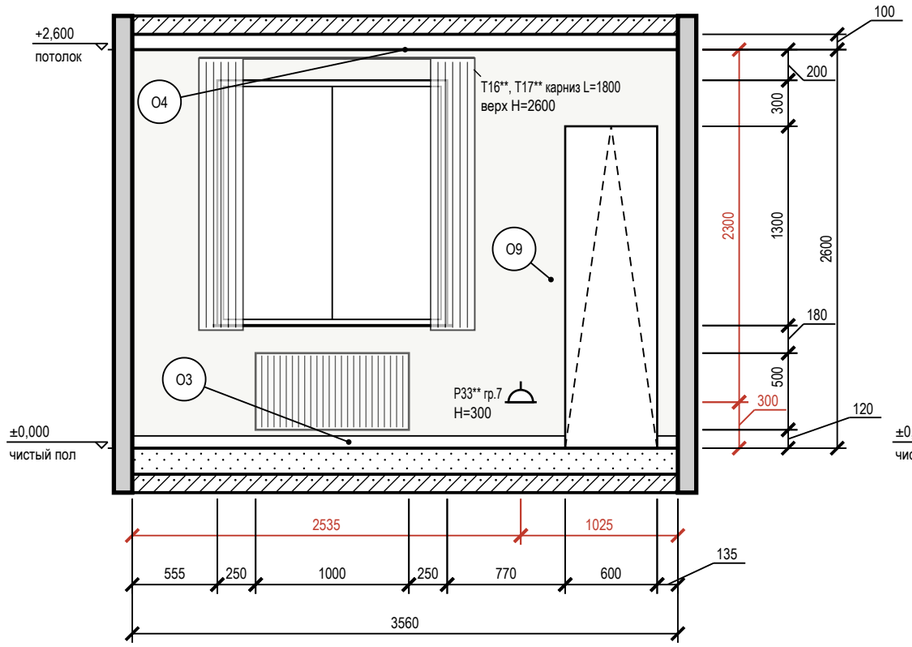

Развёртка стены Г

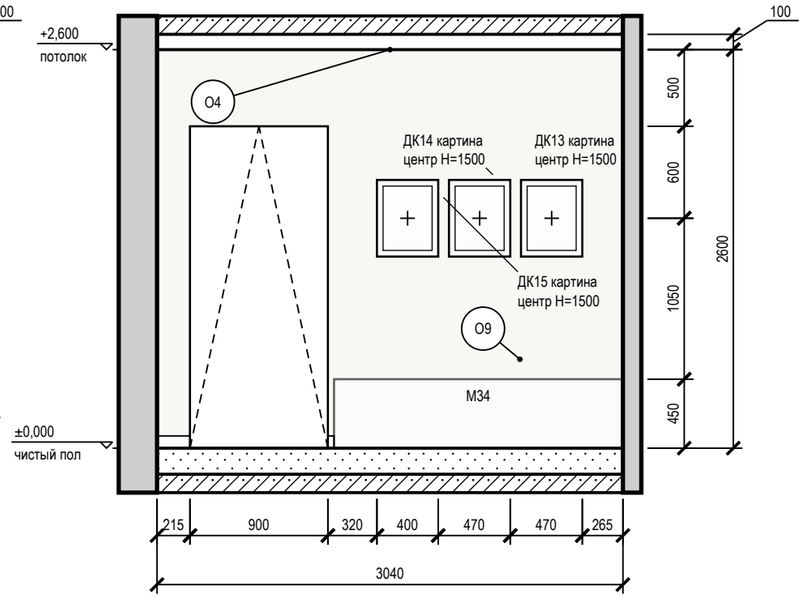

Условные обозначения

- розетка с заземляющим контактом; у знака — марка, ×N постов в рамке, гр. — группа щита, Н — высота оси, мм
- привязки точек и выводов от угла и от пола, мм
- мебель и приборы — фасад по расстановке (условно)
- картина (декор): марка Д, крест — центр, Н — высота центра, мм
- карниз (шина) и шторы в собранном виде: марка Т, длина L, верх Н
- окно: проём, рама, подоконник
- дверной проём; марка двери — в кружке
- радиатор отопления; марка — по плану отопления
- стены и перекрытия в сечении
- окраска: тон — цвет по коду производителя (условно)
- О1 — марка отделки по реестру отделки альбома
- А — марка развёртки: буква стены, стрелка — взгляд

Схема развёрток (М 1:100)

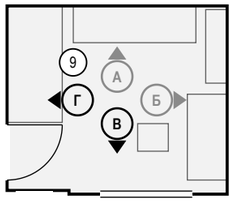

Ведомость отделки (на листе)

Марка	Поверхность	Материал, изделие	Цвет, код	Кол.
О3	плинтус	плинтус МДФ, h 80 мм, аналог: плинтус МДФ под окраску 80×16 мм, полуглянцевая	Tikkurila F497 «Paper»	3,2 м
О4	потолок	окраска, Tikkurila Anti-Reflex 2, глубокоматовая, подготовка Q3	Tikkurila F497 «Paper»	11 м²
О9	стены	окраска, Tikkurila Joker, шелковисто-матовая, подготовка К3	Tikkurila F497 «Paper»	11,6 м²

Допущения и предложения на листе

Основа листа: размеры сняты с размерных цепочек растрового скана плана заказчика, на объекте не замерены; ступени наружного контура приведены к граням помещений модели (ИЗ-8, К-20, К-21); высота потолка 2700 мм принята, источника нет (К-24); тип дома и перекрытие (монолит, плита 220 мм) приняты, источника нет (К-3); толщины стен приняты (250 и 120 мм), источника нет (К-21); мощность 15 кВт принята, технических условий нет (К-25).

Знак «**» — предложение проектировщика, заказчиком не утверждено (согласовать с заказчиком): ИЗ-1: Т16, Т17; ИЗ-1, К-1: окно пом. 9 (стена В); ИЗ-8: Р33.

См. лист открытых вопросов (лист 6, записи К-1, К-3; лист 7, записи К-20, К-21, К-24, К-25; лист 9, запись ИЗ-1; лист 10, запись ИЗ-8).

Примечания

1. Развёртки — вид на стену изнутри помещения, по часовой стрелке; расположение — на схеме листа и на листе 90; размеры — в мм по чистовым поверхностям; отметки — в м от ±0,000; высоты Н — от чистого пола помещения до оси изделия, у декора — до центра.
2. Красные цепочки — привязки электроточек и выводов: по горизонтали от угла чистовых стен, по вертикали от чистого пола, до оси изделия; звенья короче 3 мм на листе вынесены во второй ярус (ближняя к стене цепочка).
3. У знака электроточки: марка (Р — розетка, S — выключатель, Св — светильник, ЭВ — вывод кабеля), ×N — число постов в рамке, гр. — группа щита, Н — высота оси от чистого пола, мм; группы по клавишам выключателя — на листе выключателей.
4. Схема мебели, приборов и декора не является технической документацией для производства мебели; габариты — по паспортам изделий.
5. Картины и зеркала крепить к основанию по паспорту изделия (закладные и анкеры — в перечне скрытых работ); крест — ось центра предмета.
6. Карнизы (шины) — по ведомости текстиля декоратора; длина L и верх Н — по развёртке, крепление — до окраски потолка.

1000 мм · печать 1:1

Изм.	Кол.уч	Лист	№ док.	Подп.	Дата
Разраб.		Кырлан А.С.			21.10.26
Пров.					
ГИП		Кырлан А.С.			21.10.26
Н. контр.					
Утв.					

ГД-2026-004-АИ

Четырёхкомнатная квартира

Общая площадь 102,67* м² · * размеры со скана, не замерены (реестр — л. 6–11, ИЗ-8, К-20, К-21)

Дизайн-проект интерьера четырёхкомнатной квартиры

Стадия	Лист	Листов
РП	109	124

Развёртки стен В, Г. Детская 2 (пом. 9)

М 1:40

Кырлан Александр Сергеевич

выпуск 05.10.2026 № 7e7a2cd217 · стр. 120 из 168

Развёртки стен А, Б. Санузел (пом. 10)

Санузел (пом. 10) · вид изнутри помещения · размеры в мм, отметки в м

ПРЕДВАРИТЕЛЬНО · не для производства работ · открыто пунктов: 30 (реестр — л. 6–11)

Развёртка стены А

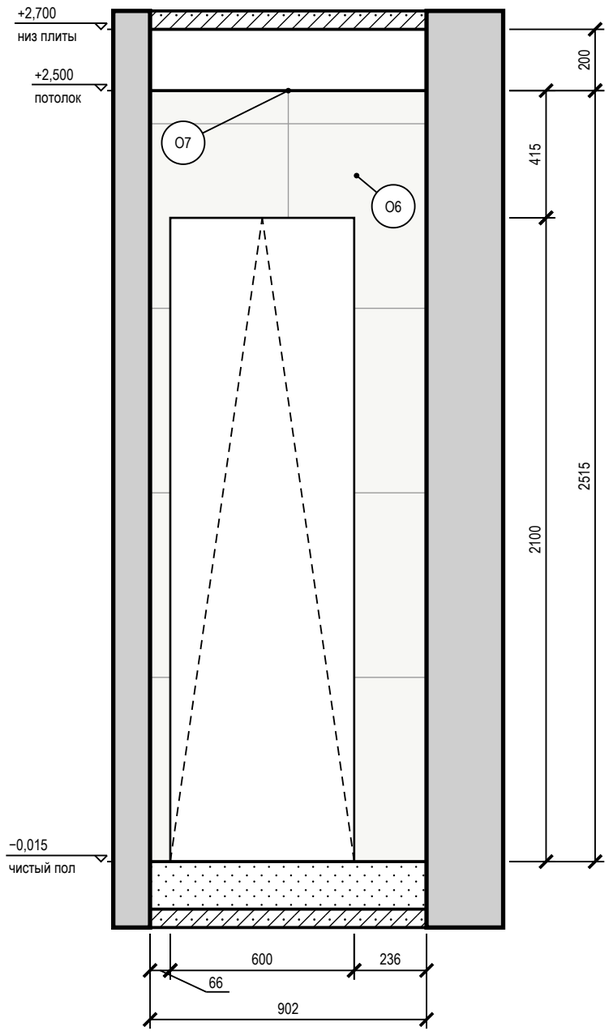

Развёртка стены Б

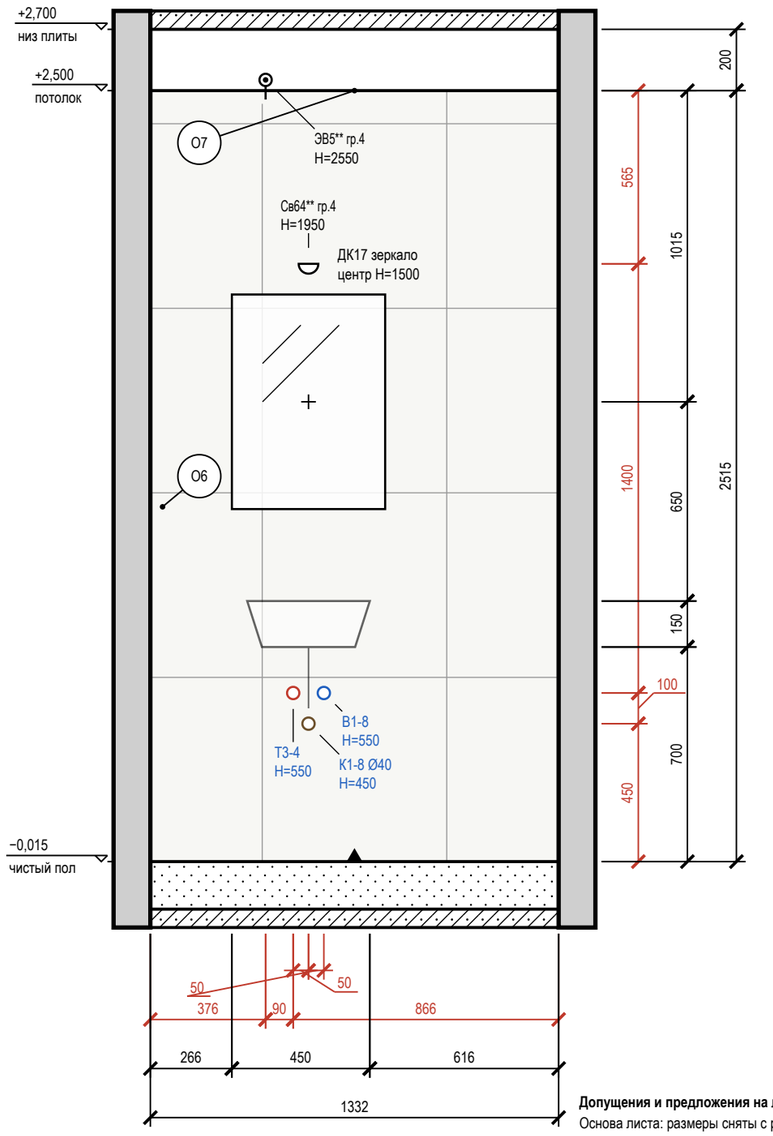

Схема развёрток (М 1:100)

Условные обозначения

- вывод кабеля для подключения прибора (без розетки), марка ЭВ
- светильник настенный (бра), H — высота оси
- вывод В1 (код — в ведомости привязок)
- вывод Т3 (код — в ведомости привязок)
- вывод К1 (код — в ведомости привязок)
- привязки точек и выводов от угла и от пола, мм
- мебель и приборы — фасад по расстановке (условно)
- зеркало: марка Д, крест — центр, H — высота центра, мм
- дверной проём; марка двери — в кружке
- стены и перекрытия в сечении
- плитка: сетка швов по формату, ▲ — ось старта
- окраска: тон — цвет по коду производителя (условно)
- О1 — марка отделки по реестру отделки альбома
- А — марка развёртки: буква стены, стрелка — взгляд

Ведомость отделки (на листе)

Марка	Поверхность	Материал, изделие	Цвет, код	Кол.
О6	стены	облицовка плиткой, 600×600×9 мм, аналог: керамогранит матовый, тон F497, затирка CG2WA	#F1F1EC «тон Paper F497»	4,4 м²
О7	потолок	окраска, Tikkurila Luja 7, матовая, подготовка Q3	Tikkurila F497 «Paper»	1,3 м²

Допущения и предложения на листе

Основа листа: размеры сняты с размерных цепочек растрового скана плана заказчика, на объекте не замерены; ступени наружного контура приведены к граням помещений модели (ИЗ-8, К-20, К-21); высота потолка 2700 мм принята, источника нет (К-24); тип дома и перекрытие (монолит, плита 220 мм) приняты, источника нет (К-3); толщины стен приняты (250 и 120 мм), источника нет (К-21); мощность 15 кВт принята, технических условий нет (К-25).

Знак «**» — предложение проектировщика, заказчиком не утверждено (согласовать с заказчиком): ИЗ-3: Св64; ИЗ-12: ЭВ5 — вывод к бытовому вентилятору, таймер выбега.

См. лист открытых вопросов (лист 6, запись К-3; лист 7, записи К-20, К-21, К-24, К-25; лист 9, запись ИЗ-3; лист 10, записи ИЗ-8, ИЗ-12).

Примечания

1. Развёртки — вид на стену изнутри помещения, по часовой стрелке; расположение — на схеме листа и на листе 90; размеры — в мм по чистовым поверхностям; отметки — в м от ±0,000; высоты H — от чистого пола помещения до оси изделия, у декора — до центра.
2. Красные цепочки — привязки электроточек и выводов: по горизонтали от угла чистовых стен, по вертикали от чистого пола, до оси изделия; звенья короче 3 мм на листе вынесены во второй ярус (ближняя к стене цепочка).
3. У знака электроточки: марка (Р — розетка, S — выключатель, Св — светильник, ЭВ — вывод кабеля), ×N — число постов в рамке, гр. — группа щита, H — высота оси от чистого пола, мм; группы по клавишам выключателя — на листе выключателей.
4. Схема мебели, приборов и декора не является технической документацией для производства мебели; габариты — по паспортам изделий.
5. Облицовка — по сетке швов 2 мм, раскладка от оси стены (треугольник у пола); подрезки — по листу раскладки плитки.
6. Гидроизоляция в 2 слоя, заход на стены 200 мм — до облицовки, с актом скрытых работ и тестом проливом (узел — на листе узлов).
7. Картины и зеркала крепить к основанию по паспорту изделия (закладные и анкеры — в перечне скрытых работ); крест — ось центра предмета.
8. Линии узора (швы плитки, складки штор, рёбра радиаторов) прерываются у знаков и выносок — просвет между линиями не менее 0,7 мм.

1000 мм · печать 1:1

Изм.	Кол.уч	Лист	№ док.	Подп.	Дата
Разраб.		Кырлан А.С.			21.10.26
Пров.					
ГИП		Кырлан А.С.			21.10.26
Н. контр.					
Утв.					

ГД-2026-004-АИ

Четырёхкомнатная квартира

Общая площадь 102,67* м² · * размеры со скана, не замерены (реестр — л. 6–11, ИЗ-8, К-20, К-21)

Дизайн-проект интерьера четырёхкомнатной квартиры

Стадия	Лист	Листов
РП	110	124

Развёртки стен А, Б. Санузел (пом. 10)

М 1:20

Кырлан Александр Сергеевич

выпуск 05.10.2026 № 7e7a2cd217 · стр. 121 из 168

Развёртки стен В, Г. Санузел (пом. 10)

Санузел (пом. 10) · вид изнутри помещения · размеры в мм, отметки в м

ПРЕДВАРИТЕЛЬНО · не для производства работ · открыто пунктов: 30 (реестр — л. 6–11)

Развёртка стены В

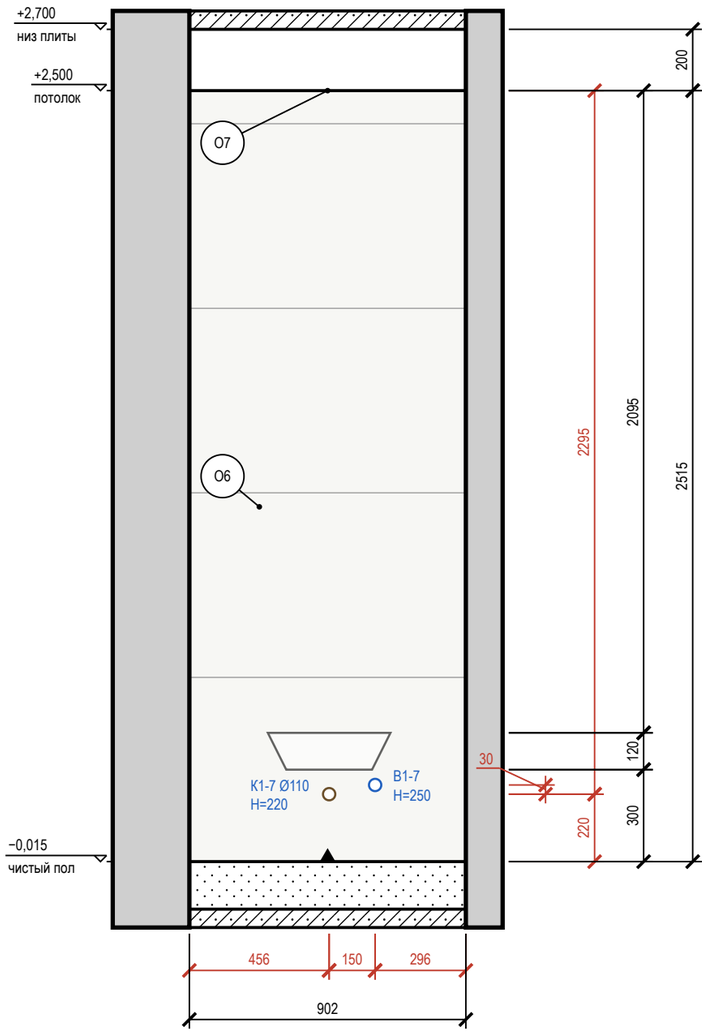

Развёртка стены Г

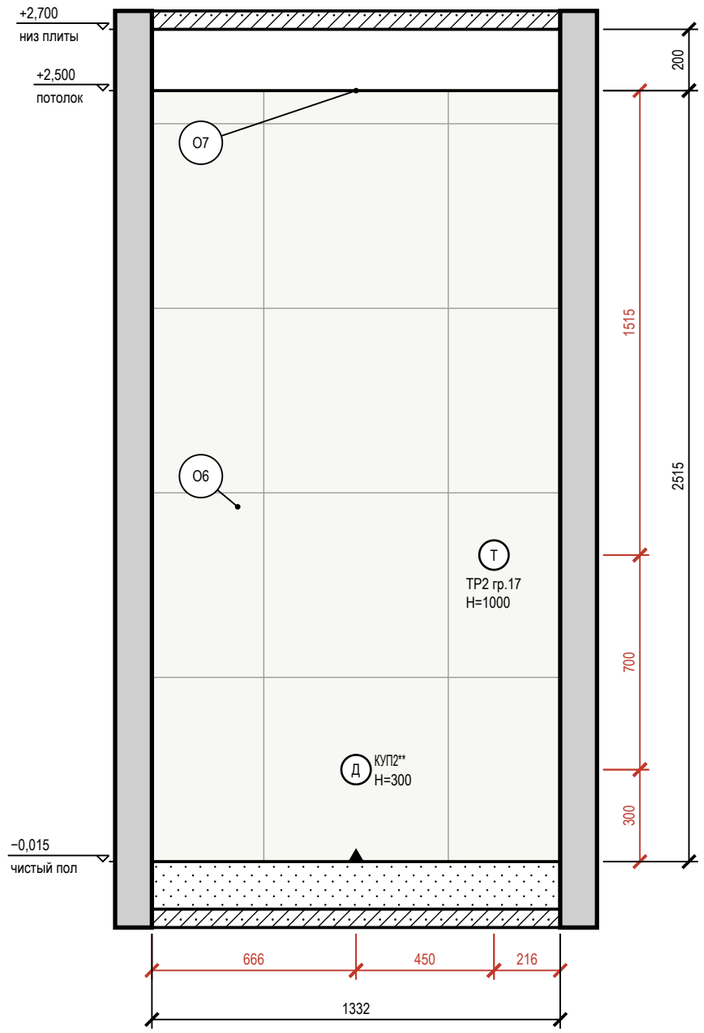

Схема развёрток (М 1:100)

Условные обозначения

- T — терморегулятор тёплого пола
- вывод В1 (код — в ведомости привязок)
- вывод К1 (код — в ведомости привязок)
- привязки точек и выводов от угла и от пола, мм
- мебель и приборы — фасад по расстановке (условно)
- стены и перекрытия в сечении
- плитка: сетка швов по формату, ▲ — ось старта
- окраска: тон — цвет по коду производителя (условно)
- О1 — марка отделки по реестру отделки альбома
- A — марка развёртки: буква стены, стрелка — взгляд

Ведомость отделки (на листе)

Марка	Поверхность	Материал, изделие	Цвет, код	Кол.
О6	стены	облицовка плиткой, 600×600×9 мм, аналог: керамогранит матовый, тон F497, затирка CG2WA	#F1F1EC «тон Paper F497»	5,6 м²
О7	потолок	окраска, Tikkurila Luja 7, матовая, подготовка Q3	Tikkurila F497 «Paper»	1,3 м²

Допущения и предложения на листе

Основа листа: размеры сняты с размерных цепочек растрового скана плана заказчика, на объекте не замерены; ступени наружного контура приведены к граням помещений модели (И3-8, К-20, К-21); высота потолка 2700 мм принята, источника нет (К-24); тип дома и перекрытие (монолит, плита 220 мм) приняты, источника нет (К-3); толщины стен приняты (250 и 120 мм), источника нет (К-21); мощность 15 кВт принята, технических условий нет (К-25).

Знак «**» — предложение проектировщика, заказчиком не утверждено (согласовать с заказчиком): И3-12: КУП2 — коробка уравнивания потенциалов, проводник от шины PE.

См. лист открытых вопросов (лист 6, запись К-3; лист 7, записи К-20, К-21, К-24, К-25; лист 10, записи И3-8, И3-12).

Примечания

1. Развёртки — вид на стену изнутри помещения, по часовой стрелке; расположение — на схеме листа и на листе 90; размеры — в мм по чистовым поверхностям; отметки — в м от ±0,000; высоты Н — от чистого пола помещения до оси изделия, у декора — до центра.
2. Красные цепочки — привязки электроточек и выводов: по горизонтали от угла чистовых стен, по вертикали от чистого пола, до оси изделия; звенья короче 3 мм на листе вынесены во второй ярус (ближняя к стене цепочка).
3. У знака электроточки: марка (Р — розетка, S — выключатель, Св — светильник, ЭВ — вывод кабеля), ×N — число постов в рамке, гр. — группа щита, Н — высота оси от чистого пола, мм; группы по клавишам выключателя — на листе выключателей.
4. Схема мебели, приборов и декора не является технической документацией для производства мебели; габариты — по паспортам изделий.
5. Облицовка — по сетке швов 2 мм, раскладка от оси стены (треугольник у пола); подрезки — по листу раскладки плитки.
6. Гидроизоляция в 2 слоя, заход на стены 200 мм — до облицовки, с актом скрытых работ и тестом проливом (узел — на листе узлов).

1000 мм · печать 1:1

Изм.	Кол.уч	Лист	№ док.	Подп.	Дата
Разраб.		Кырлан А.С.			21.10.26
Пров.					
ГИП		Кырлан А.С.			21.10.26
Н. контр.					
Утв.					

ГД-2026-004-АИ

Четырёхкомнатная квартира

Общая площадь 102,67* м² · * размеры со скана, не замерены (реестр — л. 6–11, И3-8, К-20, К-21)

Дизайн-проект интерьера четырёхкомнатной квартиры

Стадия	Лист	Листов
РП	111	124

Развёртки стен В, Г. Санузел (пом. 10)

М 1:20

Кырлан Александр Сергеевич

выпуск 05.10.2026 № 7e7a2cd217 · стр. 122 из 168

Развёртки стен А, Б. Гостиная (пом. 11)

Гостиная (пом. 11) · вид изнутри помещения · размеры в мм, отметки в м

ПРЕДВАРИТЕЛЬНО · не для производства работ · открыто пунктов: 30 (реестр — л. 6–11)

Развёртка стены А

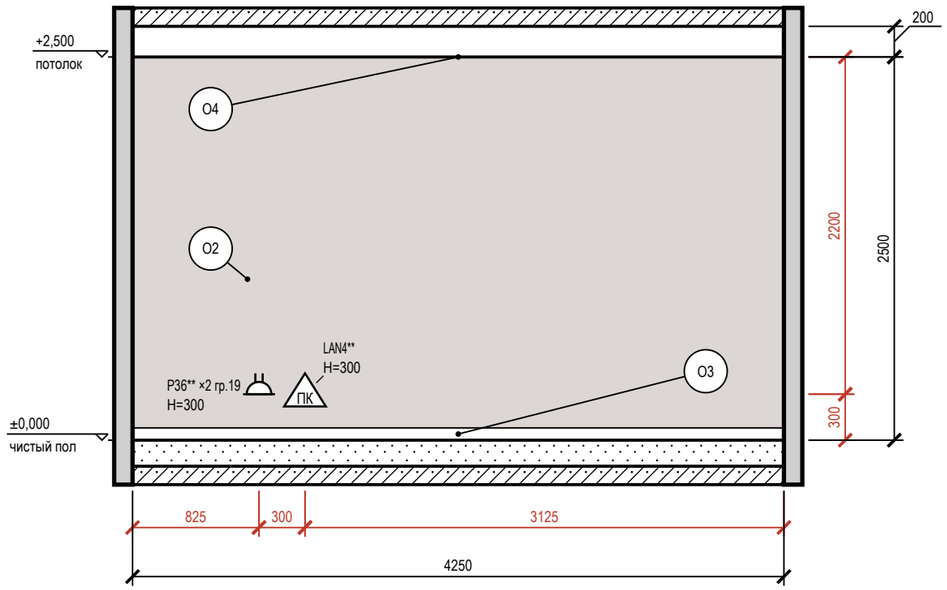

Развёртка стены Б

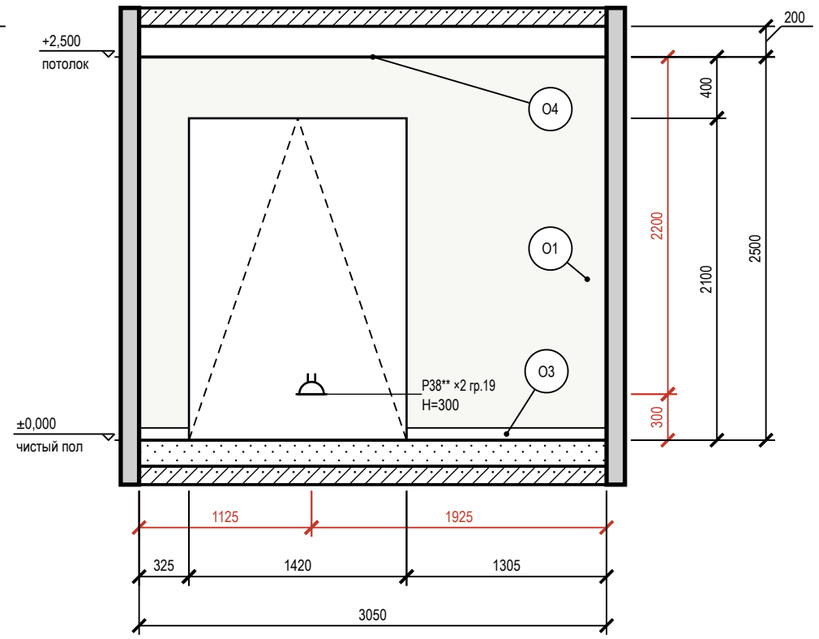

Условные обозначения

- розетка с заземляющим контактом; у знака — марка, ×N постов в рамке, гр. — группа щита, H — высота оси, мм
- ПК — розетка компьютерная RJ45
- привязки точек и выводов от угла и от пола, мм
- мебель и приборы — фасад по расстановке (условно)
- дверной проём; марка двери — в кружке
- стены и перекрытия в сечении
- окраска: тон — цвет по коду производителя (условно)
- О1 — марка отделки по реестру отделки альбома
- А — марка развёртки: буква стены, стрелка — взгляд

Схема развёрток (М 1:100)

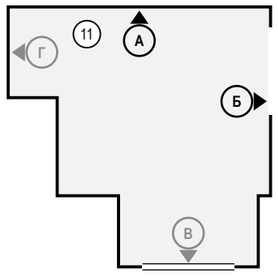

Ведомость отделки (на листе)

Марка	Поверхность	Материал, изделие	Цвет, код	Кол.
О1	стены	окраска, Tikkurila Optiva 5 Matt, матовая, подготовка К3	Tikkurila F497 «Paper»	4,6 м²
О2	акцентная стена	окраска, Tikkurila Optiva 5 Matt, аналог: интерьерная краска, класс 2 по EN 13300, глубокоматовая/матовая, база С, матовая, подготовка К3	Tikkurila L481 «Silhouette»	10,6 м²
О3	плинтус	плинтус МДФ, h 80 мм, аналог: плинтус МДФ под окраску 80×16 мм, полуглянцевая	Tikkurila F497 «Paper»	5,9 м
О4	потолок	окраска, Tikkurila Anti-Reflex 2, глубокоматовая, подготовка Q3	Tikkurila F497 «Paper»	14,6 м²

Допущения и предложения на листе

Основа листа: размеры сняты с размерных цепочек растрового скана плана заказчика, на объекте не замерены; ступени наружного контура приведены к граням помещений модели (ИЗ-8, К-20, К-21); высота потолка 2700 мм принята, источника нет (К-24); тип дома и перекрытие (монолит, плита 220 мм) приняты, источника нет (К-3); толщины стен приняты (250 и 120 мм), источника нет (К-21); мощность 15 кВт принята, технических условий нет (К-25).

Знак «*» — принято, не замерено и не подтверждено (замерить на объекте): К-22: окно пом. 11 (стена В).

Знак «**» — предложение проектировщика, заказчиком не утверждено (согласовать с заказчиком): ИЗ-5: Р36, Р38 — перенесена из группы 9 (фартук кухни) в новую группу 19 «розетки гостиной» (EL-52: в группе 9 было бы 14 гнёзд при пределе 12); ИЗ-9: LAN4.

См. лист открытых вопросов (лист 6, запись К-3; лист 7, записи К-20–К-22, К-24, К-25; лист 9, запись ИЗ-5; лист 10, записи ИЗ-8, ИЗ-9).

Примечания

1. Развёртки — вид на стену изнутри помещения, по часовой стрелке; расположение — на схеме листа и на листе 90; размеры — в мм по чистовым поверхностям; отметки — в м от ±0,000; высоты H — от чистого пола помещения до оси изделия, у декора — до центра.
2. Красные цепочки — привязки электроточек и выводов: по горизонтали от угла чистовых стен, по вертикали от чистого пола, до оси изделия; звенья короче 3 мм на листе вынесены во второй ярус (ближняя к стене цепочка).
3. У знака электроточки: марка (Р — розетка, S — выключатель, Св — светильник, ЭВ — вывод кабеля), ×N — число постов в рамке, гр. — группа щита, H — высота оси от чистого пола, мм; группы по клавишам выключателя — на листе выключателей.
4. Схема мебели, приборов и декора не является технической документацией для производства мебели; габариты — по паспортам изделий.
5. Потолок на развёртках — по нижнему уровню У1; другие уровни потолка помещения: У2 +2,600.

1000 мм · печать 1:1

Изм.	Кол.уч	Лист	№ док.	Подп.	Дата
Разраб.		Кырлан А.С.			21.10.26
Пров.					
ГИП		Кырлан А.С.			21.10.26
Н. контр.					
Утв.					

ГД-2026-004-АИ

Четырёхкомнатная квартира

Общая площадь 102,67* м² · * размеры со скана, не замерены (реестр — л. 6–11, ИЗ-8, К-20, К-21)

Дизайн-проект интерьера четырёхкомнатной квартиры

Стадия	Лист	Листов
РП	112	124

Развёртки стен А, Б. Гостиная (пом. 11)

М 1:40

Кырлан Александр Сергеевич

выпуск 05.10.2026 № 7e7a2cd217 · стр. 123 из 168

Развёртки стен В, Г. Гостиная (пом. 11)

Гостиная (пом. 11) · вид изнутри помещения · размеры в мм, отметки в м

ПРЕДВАРИТЕЛЬНО · не для производства работ · открыто пунктов: 30 (реестр — л. 6–11)

Развёртка стены В

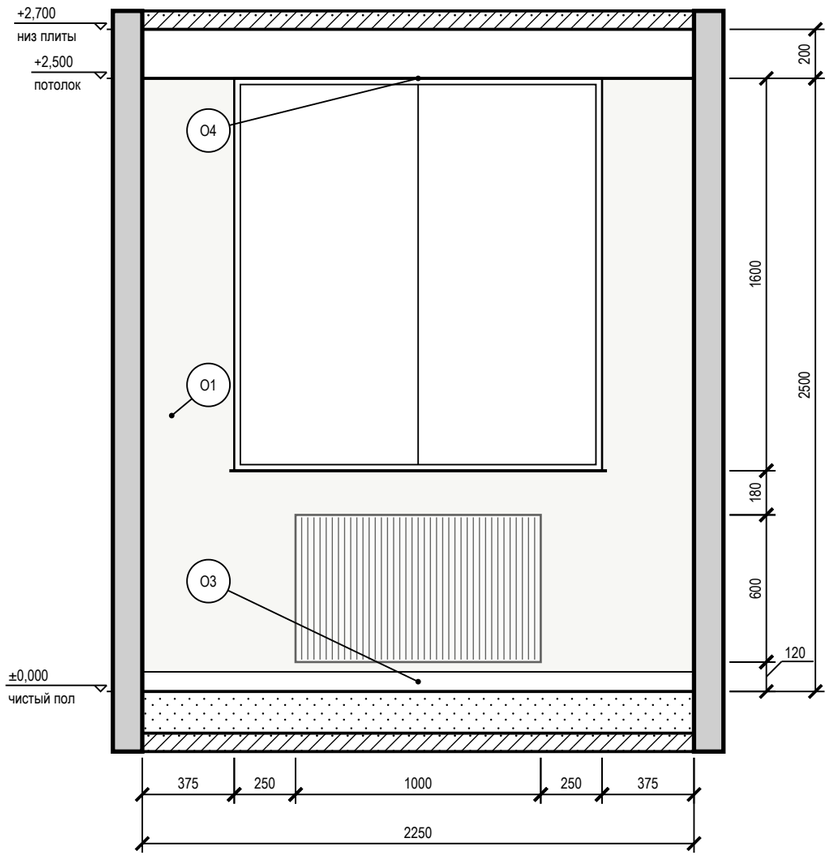

Развёртка стены Г

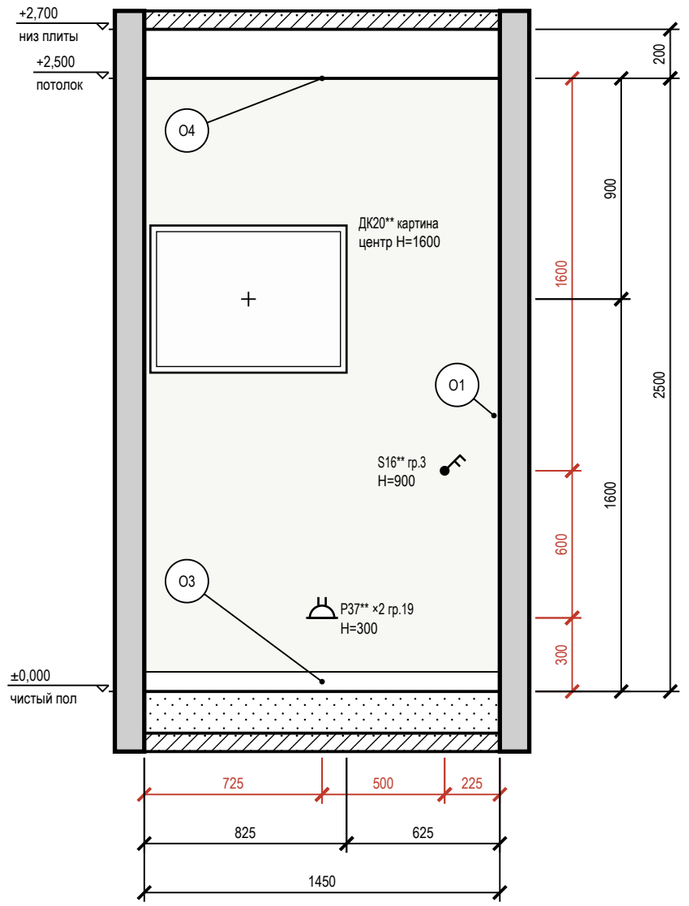

Схема развёрток (М 1:100)

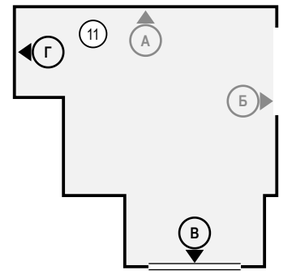

Условные обозначения

- розетка с заземляющим контактом; у знака — марка, ×N постов в рамке, гр. — группа щита, Н — высота оси, мм
- выключатель одноклавишный
- выключатель двухклавишный (флажков — по числу клавиш)
- привязки точек и выводов от угла и от пола, мм
- мебель и приборы — фасад по расстановке (условно)
- картина (декор): марка Д, крест — центр, Н — высота центра, мм
- окно: проём, рама, подоконник
- радиатор отопления; марка — по плану отопления
- стены и перекрытия в сечении
- окраска: тон — цвет по коду производителя (условно)
- О1 — марка отделки по реестру отделки альбома
- А — марка развёртки: буква стены, стрелка — взгляд

Ведомость отделки (на листе)

Марка	Поверхность	Материал, изделие	Цвет, код	Кол.
О1	стены	окраска, Tikkurila Optiva 5 Matt, матовая, подготовка К3	Tikkurila F497 «Paper»	6,8 м²
О3	плинтус	плинтус МДФ, h 80 мм, аналог: плинтус МДФ под окраску 80×16 мм, полуглянцевая	Tikkurila F497 «Paper»	3,7 м
О4	потолок	окраска, Tikkurila Anti-Reflex 2, глубокоматовая, подготовка Q3	Tikkurila F497 «Paper»	14,6 м²

Допущения и предложения на листе

Основа листа: размеры сняты с размерных цепочек растрового скана плана заказчика, на объекте не замерены; ступени наружного контура приведены к граням помещений модели (ИЗ-8, К-20, К-21); высота потолка 2700 мм принята, источника нет (К-24); тип дома и перекрытие (монолит, плита 220 мм) приняты, источника нет (К-3); толщины стен приняты (250 и 120 мм), источника нет (К-21); мощность 15 кВт принята, технических условий нет (К-25).

Знак «*» — принято, не замерено и не подтверждено (замерить на объекте): К-22: окно пом. 11 (стена В).

Знак «**» — предложение проектировщика, заказчиком не утверждено (согласовать с заказчиком): ИЗ-5: Р37 — перенесена из группы 9 (фартук кухни) в новую группу 19 «розетки гостиной» (EL-52: в группе 9 было бы 14 гнёзд при пределе 12); ИЗ-7: ДК20; S16 — вторая клавиша (подсветка картины ДК20) добавлена как предложение.

См. лист открытых вопросов (лист 6, запись К-3; лист 7, записи К-20–К-22, К-24, К-25; лист 9, записи ИЗ-5, ИЗ-7; лист 10, запись ИЗ-8).

Примечания

1. Развёртки — вид на стену изнутри помещения, по часовой стрелке; расположение — на схеме листа и на листе 90; размеры — в мм по чистовым поверхностям; отметки — в м от ±0,000; высоты Н — от чистого пола помещения до оси изделия, у декора — до центра.
2. Красные цепочки — привязки электроточек и выводов: по горизонтали от угла чистовых стен, по вертикали от чистого пола, до оси изделия; звенья короче 3 мм на листе вынесены во второй ярус (ближняя к стене цепочка).
3. У знака электроточки: марка (Р — розетка, S — выключатель, Св — светильник, ЭВ — вывод кабеля), ×N — число постов в рамке, гр. — группа щита, Н — высота оси от чистого пола, мм; группы по клавишам выключателя — на листе выключателей.
4. Схема мебели, приборов и декора не является технической документацией для производства мебели; габариты — по паспортам изделий.
5. Картины и зеркала крепить к основанию по паспорту изделия (закладные и анкеры — в перечне скрытых работ); крест — ось центра предмета.
6. Потолок на развёртках — по нижнему уровню У1; другие уровни потолка помещения: У2 +2,600.

1000 мм · печать 1:1

Изм.	Кол.уч	Лист	№ док.	Подп.	Дата			
Разраб.		Кырлан А.С.			21.10.26	ГД-2026-004-АИ		
Пров.						Четырёхкомнатная квартира Общая площадь 102,67* м² · * размеры со скана, не замерены (реестр — л. 6–11, ИЗ-8, К-20, К-21)		
ГИП		Кырлан А.С.			21.10.26	Дизайн-проект интерьера четырёхкомнатной квартиры	Стадия: РП	Лист: 113 / Листов: 124
Н. контр.						Развёртки стен В, Г. Гостиная (пом. 11) М 1:25	Кырлан Александр Сергеевич	
Утв.								

выпуск 05.10.2026 № 7e7a2cd217 · стр. 124 из 168

Развёртки стен. Гардеробная 1 (пом. 12)

Гардеробная 1 (пом. 12) · вид изнутри помещения · размеры в мм, отметки в м

ПРЕДВАРИТЕЛЬНО · не для производства работ · открыто пунктов: 30 (реестр — л. 6–11)

Развёртка стены А

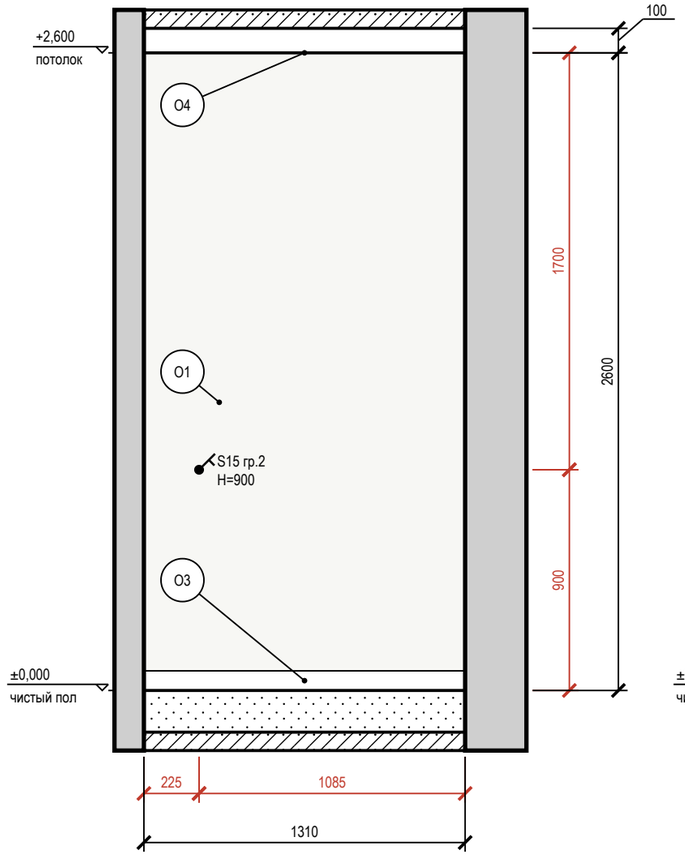

Развёртка стены Б

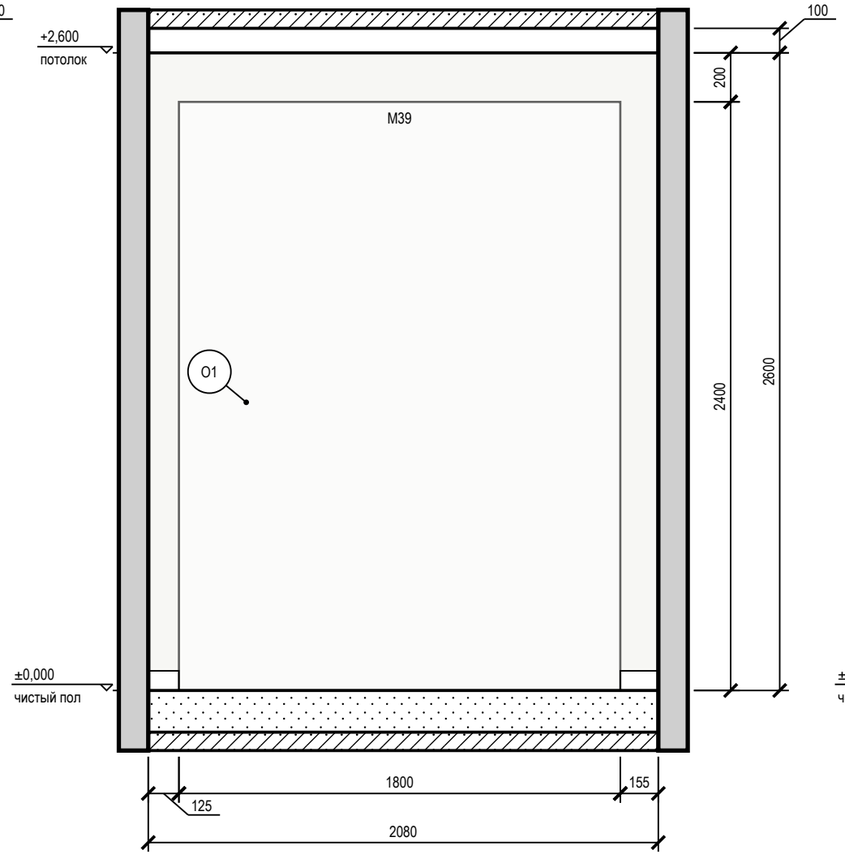

Развёртка стены В

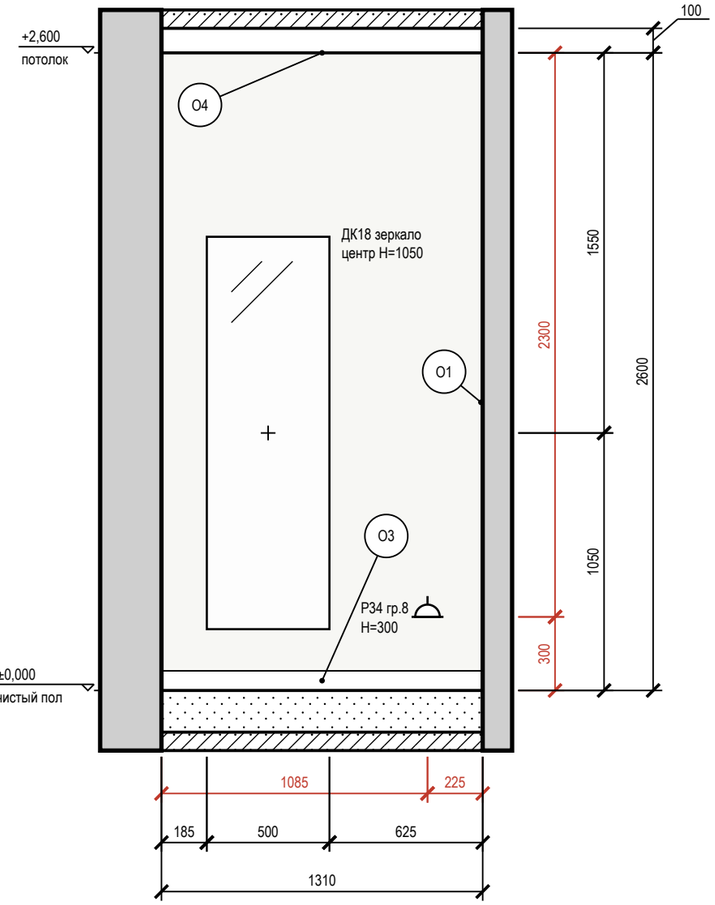

Допущения и предложения на листе. Основа листа: размеры сняты с размерных цепочек растрового скана плана заказчика, на объекте не замерены; ступени наружного контура приведены к граням помещений модели (ИЗ-8, К-20, К-21); высота потолка 2700 мм принята, источника нет (К-24); тип дома и перекрытие (монолит, плита 220 мм) приняты, источника нет (К-3); толщины стен приняты (250 и 120 мм), источника нет (К-21); мощность 15 кВт принята, технических условий нет (К-25). Знак «**» — предложение проектировщика, заказчиком не утверждено (согласовать с заказчиком): ИЗ-6: дверь пом. 12 (стена Г). См. лист открытых вопросов (лист 6, запись К-3; лист 7, записи К-20, К-21, К-24, К-25; лист 9, запись ИЗ-6; лист 10, запись ИЗ-8).

Схема развёрток (М 1:100)

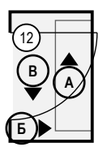

Условные обозначения

- розетка с заземляющим контактом; у знака — марка, ×N постов в рамке, гр. — группа щита, Н — высота оси, мм
- выключатель одноклавишный
- привязки точек и выводов от угла и от пола, мм
- мебель и приборы — фасад по расстановке (условно)
- зеркало: марка Д, крест — центр, Н — высота центра, мм
- стены и перекрытия в сечении
- окраска: тон — цвет по коду производителя (условно)
- О1 — марка отделки по реестру отделки альбома
- А — марка развёртки: буква стены, стрелка — взгляд

Ведомость отделки (на листе)

Марка	Поверхность	Материал, изделие	Цвет, код	Кол.
О1	стены	окраска, Tikkurila Optiva 5 Matt, матовая, подготовка К3	Tikkurila F497 «Paper»	12,2 м²
О3	плинтус	плинтус МДФ, h 80 мм, аналог: плинтус МДФ под окраску 80×16 мм, полуглянцевая	Tikkurila F497 «Paper»	2,9 м
О4	потолок	окраска, Tikkurila Anti-Reflex 2, глубокоматовая, подготовка Q3	Tikkurila F497 «Paper»	2,8 м²

Примечания

1. Развёртки — вид на стену изнутри помещения, по часовой стрелке; расположение — на схеме листа и на листе 90; размеры — в мм по чистовым поверхностям; отметки — в м от ±0,000; высоты Н — от чистого пола помещения до оси изделия, у декора — до центра.
2. Красные цепочки — привязки электроточек и выводов: по горизонтали от угла чистовых стен, по вертикали от чистого пола, до оси изделия; звенья короче 3 мм на листе вынесены во второй ярус (ближняя к стене цепочка).
3. У знака электроточки: марка (Р — розетка, S — выключатель, Св — светильник, ЭВ — вывод кабеля), ×N — число постов в рамке, гр. — группа щита, Н — высота оси от чистого пола, мм; группы по клавишам выключателя — на листе выключателей.
4. Схема мебели, приборов и декора не является технической документацией для производства мебели; габариты — по паспортам изделий.
5. Картины и зеркала крепить к основанию по паспорту изделия (закладные и анкеры — в перечне скрытых работ); крест — ось центра предмета.

1000 мм · печать 1:1

Изм.	Кол.уч	Лист	№ док.	Подп.	Дата
Разраб.		Кырлан А.С.			21.10.26
Пров.					
ГИП		Кырлан А.С.			21.10.26
Н. контр.					
Утв.					

ГД-2026-004-АИ

Четырёхкомнатная квартира

Общая площадь 102,67* м² · * размеры со скана, не замерены (реестр — л. 6–11, ИЗ-8, К-20, К-21)

Дизайн-проект интерьера четырёхкомнатной квартиры

Стадия	Лист	Листов
РП	114	124

Развёртки стен. Гардеробная 1 (пом. 12)

М 1:25

Кырлан Александр Сергеевич

выпуск 05.10.2026 № 7e7a2cd217 · стр. 125 из 168

Развёртки стен А, Б, В. Балкон 1 (пом. 13)

Балкон 1 (пом. 13) · вид изнутри помещения · размеры в мм, отметки в м

ПРЕДВАРИТЕЛЬНО · не для производства работ · открыто пунктов: 30 (реестр — л. 6–11)

Развёртка стены А

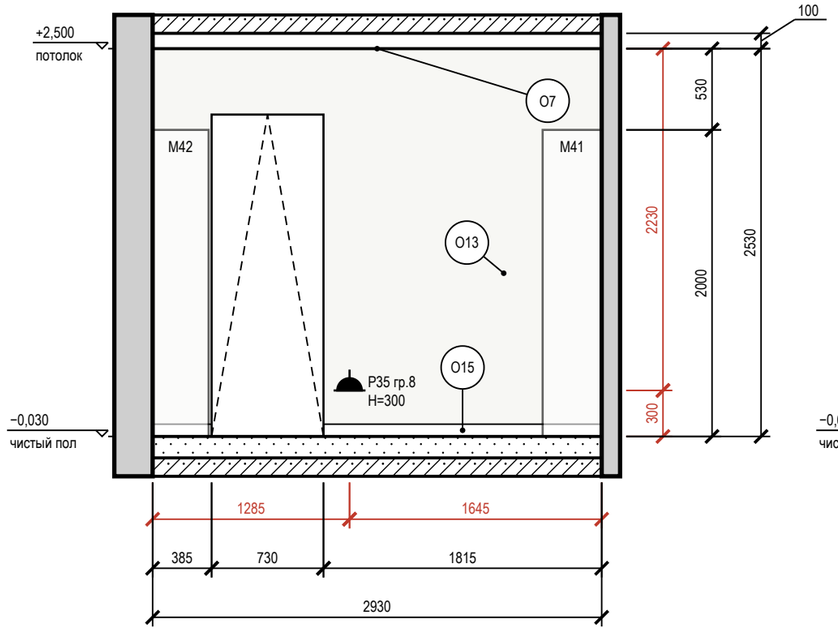

Развёртка стены Б

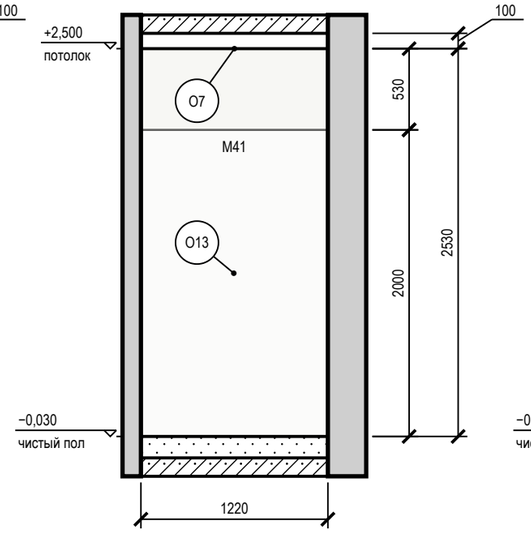

Развёртка стены В

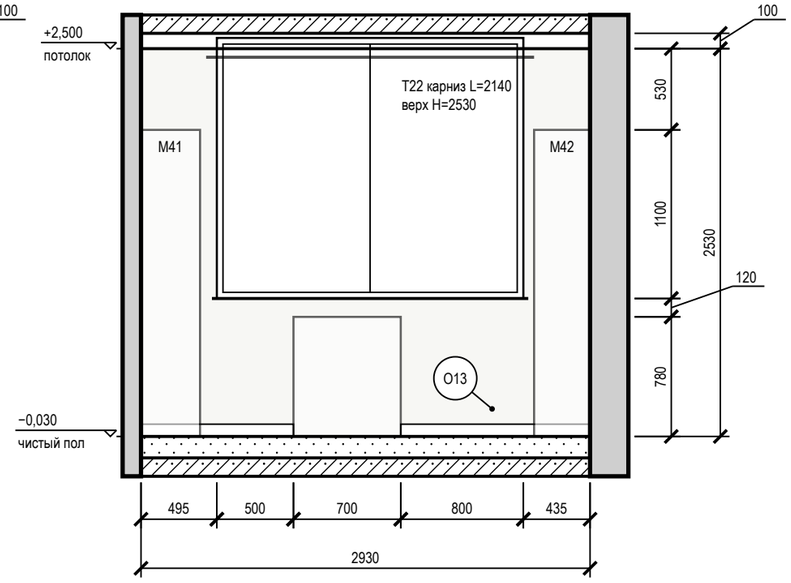

Схема развёрток (М 1:100)

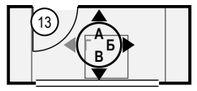

Условные обозначения

- розетка влагозащищённая IP44
- привязки точек и выводов от угла и от пола, мм
- мебель и приборы — фасад по расстановке (условно)
- карниз (шина) и шторы в собранном виде: марка T, длина L, верх H
- окно: проём, рама, подоконник
- дверной проём; марка двери — в кружке
- стены и перекрытия в сечении
- окраска: тон — цвет по коду производителя (условно)
- O1 — марка отделки по реестру отделки альбома
- A — марка развёртки: буква стены, стрелка — взгляд

Ведомость отделки (на листе)

Марка	Поверхность	Материал, изделие	Цвет, код	Кол.
O7	потолок	окраска, Tikkurila Luja 7, матовая, подготовка Q3	Tikkurila F497 «Paper»	3,7 м²
O13	стены	окраска, Tikkurila Luja 7, шелковисто-матовая, подготовка K3	Tikkurila F497 «Paper»	13,1 м²
O15	плинтус	керамогранит, аналог: плинтус из керамогранита пола, подрезка 80 мм, верхняя кромка с запилом 45°	#B8AFA5 «тон Claystone V486»	4,4 м

Допущения и предложения на листе

Основа листа: размеры сняты с размерных цепочек растрового скана плана заказчика, на объекте не замерены; ступени наружного контура приведены к граням помещений модели (ИЗ-8, К-20, К-21); высота потолка 2700 мм принята, источника нет (К-24); тип дома и перекрытие (монолит, плита 220 мм) приняты, источника нет (К-3); толщины стен приняты (250 и 120 мм), источника нет (К-21); мощность 15 кВт принята, технических условий нет (К-25).

См. лист открытых вопросов (лист 6, запись К-3; лист 7, записи К-20, К-21, К-24, К-25; лист 10, запись ИЗ-8).

Примечания

1. Развёртки — вид на стену изнутри помещения, по часовой стрелке; расположение — на схеме листа и на листе 90; размеры — в мм по чистовым поверхностям; отметки — в м от ±0,000; высоты H — от чистого пола помещения до оси изделия, у декора — до центра.
2. Красные цепочки — привязки электроточек и выводов: по горизонтали от угла чистовых стен, по вертикали от чистого пола, до оси изделия; звенья короче 3 мм на листе вынесены во второй ярус (ближняя к стене цепочка).
3. У знака электроточки: марка (Р — розетка, S — выключатель, Св — светильник, ЭВ — вывод кабеля), ×N — число постов в рамке, гр. — группа щита, H — высота оси от чистого пола, мм; группы по клавишам выключателя — на листе выключателей.
4. Схема мебели, приборов и декора не является технической документацией для производства мебели; габариты — по паспортам изделий.
5. Карнизы (шины) — по ведомости текстиля декоратора; длина L и верх H — по развёртке, крепление — до окраски потолка.

1000 мм · печать 1:1

Изм.	Кол.уч	Лист	№ док.	Подп.	Дата
Разраб.		Кырлан А.С.			21.10.26
Пров.					
ГИП		Кырлан А.С.			21.10.26
Н. контр.					
Утв.					

ГД-2026-004-АИ

Четырёхкомнатная квартира

Общая площадь 102,67* м² · * размеры со скана, не замерены (реестр — л. 6–11, ИЗ-8, К-20, К-21)

Дизайн-проект интерьера четырёхкомнатной квартиры

Стадия	Лист	Листов
РП	115	124

Развёртки стен А, Б, В. Балкон 1 (пом. 13)

М 1:40

Кырлан Александр Сергеевич

выпуск 05.10.2026 № 7e7a2cd217 · стр. 126 из 168

Развёртка стены Г. Балкон 1 (пом. 13)

Балкон 1 (пом. 13) · вид изнутри помещения · размеры в мм, отметки в м

ПРЕДВАРИТЕЛЬНО · не для производства работ · открыто пунктов: 30 (реестр — л. 6–11)

Развёртка стены Г

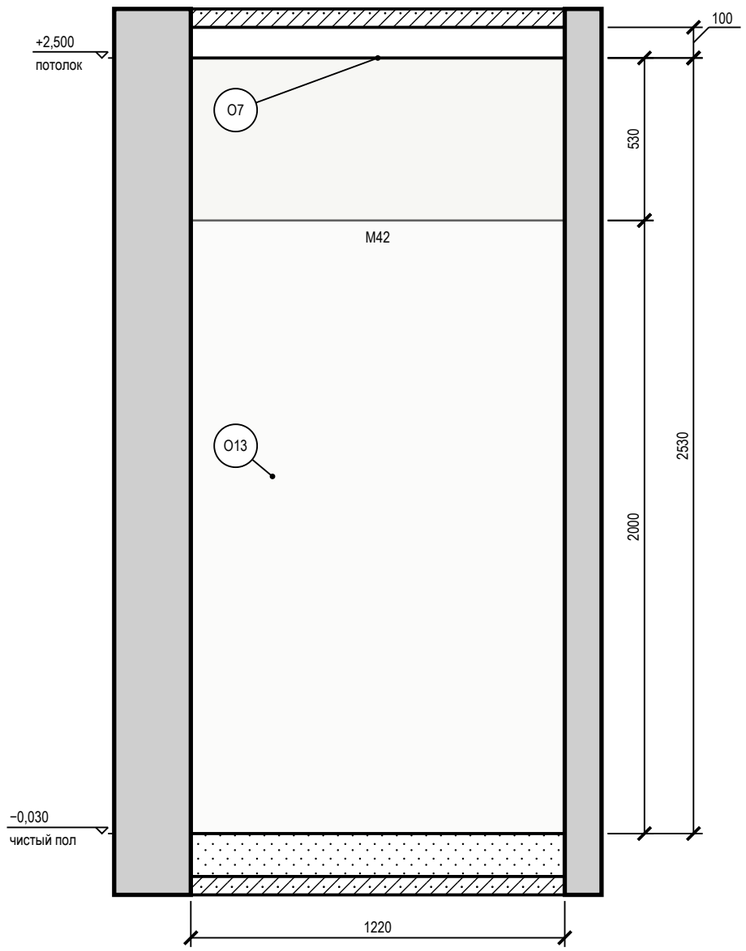

Схема развёрток (М 1:100)

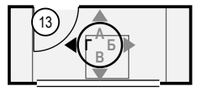

Условные обозначения

- привязки точек и выводов от угла и от пола, мм
- мебель и приборы — фасад по расстановке (условно)
- стены и перекрытия в сечении
- окраска: тон — цвет по коду производителя (условно)
- О1 — марка отделки по реестру отделки альбома
- А — марка развёртки: буква стены, стрелка — взгляд

Ведомость отделки (на листе)

Марка	Поверхность	Материал, изделие	Цвет, код	Кол.
О7	потолок	окраска, Tikkurila Luja 7, матовая, подготовка Q3	Tikkurila F497 «Paper»	3,7 м²
О13	стены	окраска, Tikkurila Luja 7, шелковисто-матовая, подготовка К3	Tikkurila F497 «Paper»	3,1 м²

Допущения и предложения на листе

Основа листа: размеры сняты с размерных цепочек растрового скана плана заказчика, на объекте не замерены; ступени наружного контура приведены к граням помещений модели (ИЗ-8, К-20, К-21); высота потолка 2700 мм принята, источника нет (К-24); тип дома и перекрытие (монолит, плита 220 мм) приняты, источника нет (К-3); толщины стен приняты (250 и 120 мм), источника нет (К-21); мощность 15 кВт принята, технических условий нет (К-25).

См. лист открытых вопросов (лист 6, запись К-3; лист 7, записи К-20, К-21, К-24, К-25; лист 10, запись ИЗ-8).

Примечания

1. Развёртки — вид на стену изнутри помещения, по часовой стрелке; расположение — на схеме листа и на листе 90; размеры — в мм по чистовым поверхностям; отметки — в м от ±0,000; высоты Н — от чистого пола помещения до оси изделия, у декора — до центра.
2. Красные цепочки — привязки электроточек и выводов: по горизонтали от угла чистовых стен, по вертикали от чистого пола, до оси изделия; звенья короче 3 мм на листе вынесены во второй ярус (ближняя к стене цепочка).
3. У знака электроточки: марка (Р — розетка, S — выключатель, Св — светильник, ЭВ — вывод кабеля), ×N — число постов в рамке, гр. — группа щита, Н — высота оси от чистого пола, мм; группы по клавишам выключателя — на листе выключателей.
4. Схема мебели, приборов и декора не является технической документацией для производства мебели; габариты — по паспортам изделий.

1000 мм · печать 1:1

Изм.	Кол.уч	Лист	№ док.	Подп.	Дата
Разраб.		Кырлан А.С.			21.10.26
Пров.					
ГИП		Кырлан А.С.			21.10.26
Н. контр.					
Утв.					

ГД-2026-004-АИ

Четырёхкомнатная квартира

Общая площадь 102,67* м² · * размеры со скана, не замерены (реестр — л. 6–11, ИЗ-8, К-20, К-21)

Дизайн-проект интерьера четырёхкомнатной квартиры

Стадия	Лист	Листов
РП	116	124

Развёртка стены Г. Балкон 1 (пом. 13)

М 1:20

Кырлан Александр Сергеевич

выпуск 05.10.2026 № 7e7a2cd217 · стр. 127 из 168

Узлы

Пороги и стыки покрытий, скрытые двери, короба стояков, гидроизоляция, плинтус

1 Порог 15 мм: мокрая зона — жилое помещение (М 1:5)

Применение: двери; места — лист 90

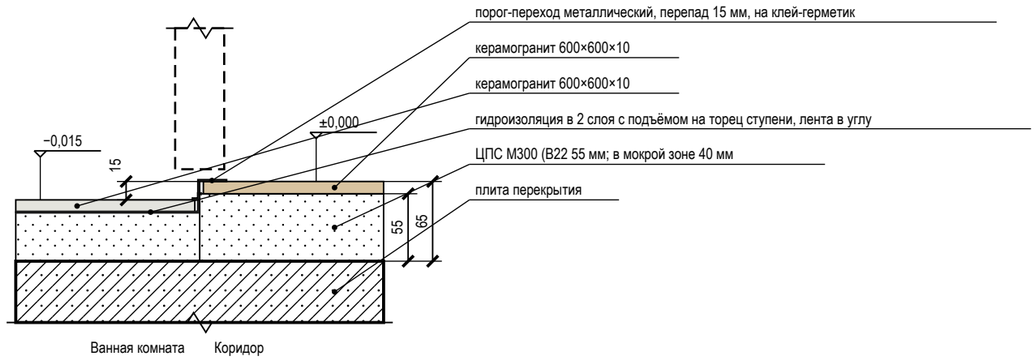

2 Стык покрытий пола Т-профилем без перепада (М 1:5)

Применение: проёмы 3↔5, 4↔5, 6↔7, 7↔8, 8↔7, 9↔7; места — лист 90

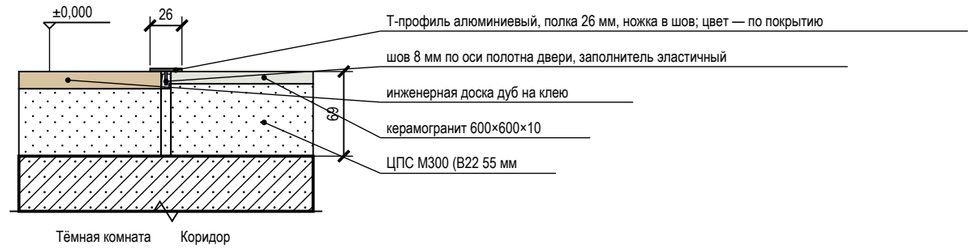

3 Короб стояков К1-1, В1-1, Т3-1 с люком и звукоизоляцией (М 1:20)

Применение: пом. 9; места — лист 90

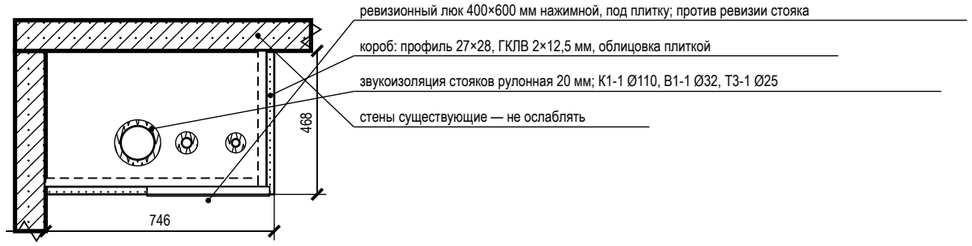

4 Гидроизоляция санузла: заход на стены 200 мм, примыкание ванны (М 1:20)

Применение: пом. 2, 10; места — лист 90

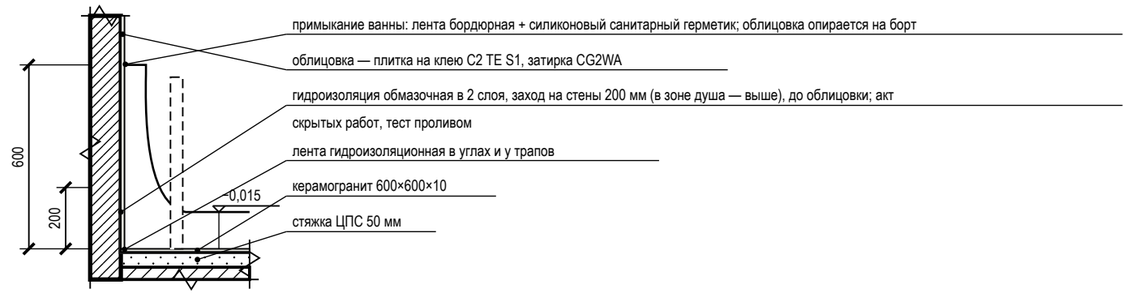

5 Плинтус МДФ 80×16 мм у окрашенной стены (М 1:10)

Применение: пом. 1, 3, 4, 5, 6, 7, 8, 9, 11, 12; места — лист 90

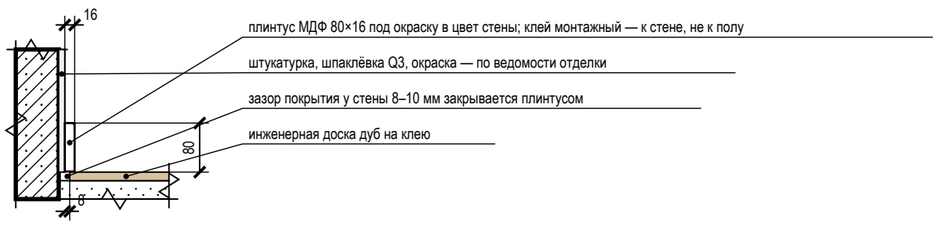

Условные обозначения

- железобетон (плита, стены)
- кладка, перегородка
- стяжка, раствор
- гипсокартон ГКЛВ
- звукоизоляция, эластичный заполнитель
- плитка, керамогранит на клею
- инженерная доска (покрытие пола)
- металлический профиль (порог, Т-профиль, короб двери)
- гидроизоляция (обмазочная, лента)

Примечания

1. Узлы — типовые решения проекта для мест, отмеченных выносками на листе схемы расположения развёрток и узлов; размеры — в мм, отметки — в м от ±0,000.
2. Узлы с гидроизоляцией, закладными и коробами скрытого монтажа принимаются по актам скрытых работ до закрытия отделкой; гидроизоляция — после теста проливом (24 ч).
3. Марки изделий (порог, Т-профиль, короб скрытой двери, люк) — по спецификациям; замена — на аналог с теми же габаритами по согласованию с автором проекта.

Допущения и предложения на листе

Основа листа: размеры сняты с размерных цепочек растрового скана плана заказчика, на объекте не замерены; ступени наружного контура приведены к граням помещений модели (ИЗ-8, К-20, К-21); высота потолка 2700 мм принята, источника нет (К-24); тип дома и перекрытие (монолит, плита 220 мм) приняты, источника нет (К-3); толщины стен приняты (250 и 120 мм), источника нет (К-21); мощность 15 кВт принята, технических условий нет (К-25).

См. лист открытых вопросов (лист 6, запись К-3; лист 7, записи К-20, К-21, К-24, К-25; лист 10, запись ИЗ-8).

Изм.	Кол.уч	Лист	№ док.	Подп.	Дата
Разраб.		Кырлан А.С.			21.10.26
Пров.					
ГИП		Кырлан А.С.			21.10.26
Н. контр.					
Утв.					

ГД-2026-004-АИ

Четырёхкомнатная квартира

Общая площадь 102,67* м² · * размеры со скана, не замерены (реестр — л. 6–11, ИЗ-8, К-20, К-21)

Дизайн-проект интерьера четырёхкомнатной квартиры

Стадия	Лист	Листов
РП	117	124

Узлы

М б/м

Кырлан Александр Сергеевич

выпуск 05.10.2026 № 7e7a2cd217 · стр. 128 из 168

10

Смета

Кырлан Александр Сергеевич

выпуск 05.10.2026 · 7e7a2cd217 · стр. 129 из 168

Ведомость объёмов работ

ПРЕДВАРИТЕЛЬНО · не для производства работ · открыто пунктов: 30 (реестр — л. 6–11)

Объёмы по помещениям от чертежа · площади в м², длины в м · формула, правило проёмов и источник в каждой строке

Ведомость объёмов работ по помещениям

Поз.	Наименование работ (материал, число слоёв)	Ед. изм.	Объём по помещениям (№ по экспликации)													Всего	Формула подсчёта	Правило проёмов	Источник	Цена за ед., ₽	Стоимость, ₽
			1	2	3	4	5	6	7	8	9	10	11	12	13						
1. Демонтаж и черновые работы																					
1	Демонтаж существующего покрытия пола до основания	м²	18,16	5,57	2,96	17,51	4,54	15,19	7,80	1,29	10,96	1,31	14,55	2,83	3,70	106,37	S пом.		л. 20, 21	по КП	
2	Демонтаж существующей отделки стен до основания	м²	39,49	22,35	16,94	40,12	22,21	35,59	23,80	8,65	29,08	10,46	37,22	14,96	16,51	317,38	P × H − проёмы	за вычетом проёмов	л. 20, 21	по КП	
3	Демонтаж существующей отделки потолка до основания	м²	18,16	5,57	2,96	17,51	4,54	15,19	7,80	1,29	10,96	1,31	14,55	2,83	3,70	106,37	S пом.		л. 20, 21	по КП	
4	Демонтаж существующих дверных блоков	шт	1	1	1	1	1	1	1	1	1	1		1	1	12	по ведомости проёмов		л. 21, 22	по КП	
5	Демонтаж существующих сантехприборов и электрооборудования (если есть)	компл															по факту на объекте		л. 21	по КП	
6	Устройство стяжки: стяжка ЦПС М300 (В22,5), фибра, по звукоизоляции, 55 мм	м²	18,21		3,00	17,56	4,68	15,30	7,95	1,39	11,05		14,64	2,92		96,70	S пом. + S в дверных проёмах (b × t/2)	проёмы добавлены	л. 53, 55–57	530	51 251
7	Гидроизоляция обмазочная, 2 слоя: пол, стены на 200 мм, зоны замачивания	м²		12,76								1,98				14,74	пол + (P − двери) × h заведения + зоны замачивания		л. 49	450	6 633
8	Штукатурка стен по маякам, до 10 мм	м²	39,49	22,35	16,94	40,12	22,21	35,59	23,80	8,65	29,08	10,46	37,22	14,96	16,51	317,38	P × H − проёмы по обводу коробок − грани перегородок на ГКЛВ	за вычетом проёмов	л. 20, 55–57	530	168 211
9	Штукатурка оконных откосов шириной до 200 мм	м²	0,85			0,85		0,71			0,85		0,24		0,97	4,47	Σ (2h + b) × глубина откоса	откосы ≤ 200 мм	л. 20	540	2 414
10	Потолок ГКЛ по каркасу П113, 1 слой	м²	18,16	5,57	2,96	17,51	4,54	15,19	7,80	1,29	10,96	1,31	14,55	2,83	3,70	106,37	S пом. по плану потолков		л. 44–48	1 500	159 555
Итого по разделу 1 — 388 064 ₽ (позиций 10, из них по КП 5); в сводную смету — л. 123, 124																					
2. Инженерные системы																					
11	Прокладка кабеля ВВГнг(А)-LS по группам щита: за потолком и в штробах стен (штробы — только после технического заключения, см. строку «Штробы в стенах»)	м														521,00	Σ длин групп щита		л. 34, 35	60	31 260
12	Прокладка слаботочной линии: Кабель коаксиальный RG-6 (75 Ом) к розеткам ТВ, отдельно от силовых	м														14,50	по лучам от ЩС**: 1 точ., запас 10 %		л. 37	по КП	
13	Прокладка слаботочной линии: Кабель U/UTP кат. 6 (LAN, Wi-Fi и камеры по PoE), отдельно от силовых	м														70,70	по лучам от ЩС**: 6 точ., запас 10 %		л. 37	по КП	
14	Прокладка гофротрубы Ø20 для слаботочных линий, отдельно от силовых	м														76,70	по длине лучей без участков в канале плинтуса (≈ 90 %)		л. 37	по КП	
15	Сборка слаботочного щита ЩС**: корпус, патч-панель, подключение линий и питания 220 В; коммутатор и точки доступа — оборудование заказчика	шт														1	один щит		л. 32, 33, 37	по КП	
16	Электроточка: подрозетник в бетоне, розетка, выключатель, вывод	шт	10	4	1	7	4	16	8		8	1	6	2	1	68	по ведомости электроточек		л. 29, 32, 33	950	64 600
17	Штробы в стенах под спуски кабеля к точкам — выполняются только после технического заключения о несущих стенах	м	18,20	5,40	2,30	13,05	7,40	23,25	12,40		14,55		10,40	4,00	2,23	113,18	Σ (H − h) по точкам на стенах: вертикальные спуски	после техзаключения	л. 21, 29	по КП	
18	Установка встраиваемого точечного светильника	шт	8	3	1	10	3	7	4	1	6	1	9	2	1	56	по плану освещения		л. 30	750	42 000
19	Монтаж светильника: потолочного, подвесного, настенного	шт	1	1		2					2	1				7	по плану освещения		л. 30	1 200	8 400
20	Монтаж LED-ленты в алюминиевый профиль	м	5,40					1,20								6,60	Σ длин лент по плану освещения		л. 30	230	1 518
21	Установка блока питания LED в доступном месте (люк, шкаф)	шт	1					1								2	один на LED-группу		л. 30	570	1 140
22	Установка автономного пожарного извещателя	шт	1			1	1	1	1		1		1			7	по плану розеток		л. 29	по КП	

Допущения и предложения на листе

Основа листа: размеры сняты с размерных цепочек растрового скана плана заказчика, на объекте не замерены; ступени наружного контура приведены к граням помещений модели (ИЗ-8, К-20, К-21); высота потолка 2700 мм принята, источника нет (К-24); тип дома и перекрытие (монолит, плита 220 мм) приняты, источника нет (К-3); толщины стен приняты (250 и 120 мм), источника нет (К-21); мощность 15 кВт принята, технических условий нет (К-25).

Знак «**» — предложение проектировщика, заказчиком не утверждено (согласовать с заказчиком): ИЗ-9: ЩС — щит слаботочный: место и состав.

См. лист открытых вопросов (лист 6, запись К-3; лист 7, записи К-20, К-21, К-24, К-25; лист 10, записи ИЗ-8, ИЗ-9).

Изм.	Кол.уч	Лист	№ док.	Подп.	Дата
Разраб.		Кырлан А.С.			21.10.26
Пров.					
ГИП		Кырлан А.С.			21.10.26
Н. контр.					
Утв.					

ГД-2026-004-АИ

Четырёхкомнатная квартира

Общая площадь 102,67* м² · * размеры со скана, не замерены (реестр — л. 6–11, ИЗ-8, К-20, К-21)

Дизайн-проект интерьера четырёхкомнатной квартиры

Стадия	Лист	Листов
РП	118	124

Ведомость объёмов работ

М б/м

Кырлан Александр Сергеевич

Ведомость объёмов работ (продолжение)

Объёмы по помещениям от чертежа · площади в м², длины в м · формула, правило проёмов и источник в каждой строке

Ведомость объёмов работ по помещениям (продолжение)

Поз.	Наименование работ (материал, число слоёв)	Ед. изм.	Объём по помещениям (№ по экспликации)													Всего	Формула подсчёта	Правило проёмов	Источник	Цена за ед., ₽	Стоимость, ₽
			1	2	3	4	5	6	7	8	9	10	11	12	13						
23	Сборка щита: установка автоматов и АВДТ групп, вводного автомата	шт														20	группы + вводной автомат		л. 34, 35	230	4 600
24	Установка вводного УЗО	шт														1	по однолинейной схеме		л. 34, 35	380	380
25	Монтаж инсталляции, установка подвесного унитаза и кнопки смыва	шт		1								1				2	по плану выводов		л. 40, 42	10 500	21 000
26	Короб инсталляции: каркас и обшивка ГКЛВ в 2 слоя, ревизионный доступ к смыву	шт		1								1				2	по плану выводов		л. 40, 49–52	по КП	
27	Короб К1 над чистым полом: каркас и обшивка ГКЛВ под плитку (материалы — в спецификации ВК)	м.п.		0,62				4,30				1,24				6,16	Σ открытых участков выпусков К1 (профиль листа разводки ВК)		л. 40, 42	по КП	
28	Установка ванны с сифоном	шт		1												1	по плану выводов		л. 40, 42	6 000	6 000
29	Установка умывальника (мойки) с сифоном и смесителем	шт		1				1				1				3	по плану выводов		л. 40, 42	3 000	9 000
30	Подключение стиральной (посудомоечной) машины к ВК	шт		1				1								2	по плану выводов		л. 40	по КП	
31	Установка радиатора с узлом подключения и терморегулятором	шт	1			1		1			1		1			5	по плану отопления		л. 39	по КП	
32	Электрический тёплый пол: укладка нагревательного мата в слой клея, датчик пола в гофротрубе	м²		1,37								0,30				1,67	Σ контуров по плану ЭОМ (полезная площадь)		л. 29, 53	750	1 253
33	Установка терморегулятора тёплого пола с датчиком в гофротрубе	шт		1								1				2	один на контур		л. 29	750	1 500
Итого по разделу 2 — 192 651 ₽ (позиций 23, из них по КП 10); в сводную смету — л. 123, 124																					
3. Чистовые работы																					
34	Облицовка стен керамогранитом 600,8×600,8 на клею	м²		21,66								9,44				31,10	по раскладке: зона облицовки − место за коробом	за вычетом проёмов	л. 49–52	2 500	77 750
35	Облицовка короба инсталляции (ГКЛВ) керамогранитом: лицо, боковины, полка	м²		1,36								1,76				3,12	по раскладке: лицо, боковины, полка		л. 49–52	2 500	7 800
36	Облицовка фартука керамогранитом 600,8×600,8	м²						1,11								1,11	по раскладке фартука		л. 49–52, 55–57	2 400	2 664
37	Укладка керамогранита на пол, 600×600, на клею	м²		5,61			4,68		7,95			1,35			3,74	23,33	S пом. + S в дверных проёмах	проёмы добавлены	л. 49–53	1 800	41 994
38	Затирка швов керамогранита	м²		28,59			4,54	1,11	7,80			12,51			3,70	58,25	Σ S облицовки и пола из плитки		л. 49–52	150	8 738
39	Грунтование стен, 2 слоя (под штукатурку и под отделку)	м²	39,49	22,35	16,94	40,12	22,21	35,59	23,80	8,65	29,08	10,46	37,22	14,96	16,51	317,38	P × H − проёмы	за вычетом проёмов	л. 55–57	96	30 468
40	Шпаклёвка стен под окраску, 2 слоя (старт и финиш), уровень К3	м²	39,49		16,94	40,12	22,21	34,48	23,80	8,65	29,08		37,22	14,96	16,51	283,46	P × H − проёмы − фартук	за вычетом проёмов	л. 55–57	750	212 595
41	Грунтование и шпаклёвка оконных откосов, 2 слоя	м.п.	4,75			4,73		3,93			4,70		4,70		5,40	28,21	Σ (2h + b) по окнам	по окнам	л. 20	300	8 463
42	Грунтование потолка, 2 слоя	м²	18,16	5,57	2,96	17,51	4,54	15,19	7,80	1,29	10,96	1,31	14,55	2,83	3,70	106,37	S пом.		л. 55–57	96	10 212
43	Шпаклёвка потолка под окраску, 2 слоя, уровень Q3	м²	18,16	5,57	2,96	17,51	4,54	15,19	7,80	1,29	10,96	1,31	14,55	2,83	3,70	106,37	S пом.		л. 44–48, 55–57	950	101 052
44	Окраска потолка водно-дисперсионной краской, 2 слоя	м²	18,16	5,57	2,96	17,51	4,54	15,19	7,80	1,29	10,96	1,31	14,55	2,83	3,70	106,37	S пом.		л. 55–57	360	38 293
45	Окраска стен водно-дисперсионной краской, 2 слоя	м²	43,85		18,41	44,46	27,04	39,42	29,05	12,01	34,63		42,60	17,94	21,30	330,71	P × H − фартук, проёмы не вычитаются	без вычета проёмов	л. 55–57	300	99 213
46	Окраска оконных откосов, 2 слоя	м.п.	4,75			4,73		3,93			4,70		4,70		5,40	28,21	Σ (2h + b) по окнам	по окнам	л. 20	120	3 385
47	Укладка инженерной доски на клей	м²	18,21		3,00	17,56		15,30		1,39	11,05		14,64	2,92		84,07	S пом. + S в дверных проёмах	проёмы добавлены	л. 53, 55–57	1 200	100 884

Допущения и предложения на листе

Основа листа: размеры сняты с размерных цепочек растрового скана плана заказчика, на объекте не замерены; ступени наружного контура приведены к граням помещений модели (ИЗ-8, К-20, К-21); высота потолка 2700 мм принята, источника нет (К-24); тип дома и перекрытие (монолит, плита 220 мм) приняты, источника нет (К-3); толщины стен приняты (250 и 120 мм), источника нет (К-21); мощность 15 кВт принята, технических условий нет (К-25).

См. лист открытых вопросов (лист 6, запись К-3; лист 7, записи К-20, К-21, К-24, К-25; лист 10, запись ИЗ-8).

Изм.	Кол.уч	Лист	№ док.	Подп.	Дата
Разраб.		Кырлан А.С.			21.10.26
Пров.					
ГИП		Кырлан А.С.			21.10.26
Н. контр.					
Утв.					

ГД-2026-004-АИ

Четырёхкомнатная квартира

Общая площадь 102,67* м² · * размеры со скана, не замерены (реестр — л. 6–11, ИЗ-8, К-20, К-21)

Дизайн-проект интерьера четырёхкомнатной квартиры

Стадия	Лист	Листов
РП	119	124

Ведомость объёмов работ (продолжение)

М б/м

Кырлан Александр Сергеевич

Ведомость объёмов работ (окончание)

Объёмы по помещениям от чертежа · площади в м², длины в м · формула, правило проёмов и источник в каждой строке

Ведомость объёмов работ по помещениям (продолжение)

Поз.	Наименование работ (материал, число слоёв)	Ед. изм.	Объём по помещениям (№ по экспликации)													Всего	Формула подсчёта	Правило проёмов	Источник	Цена за ед., ₽	Стоимость, ₽
			1	2	3	4	5	6	7	8	9	10	11	12	13						
48	Установка плинтуса МДФ h=80 мм	м.п.	16,64		6,38	16,20	8,10	13,79	8,67	3,26	11,82		15,62	5,48		105,96	P − ширина дверных проёмов		л. 55–57	450	47 682
49	Плинтус из керамогранита: нарезка полос из плитки пола, запил кромки 45°, установка h=80 мм	м.п.													7,69	7,69	P − ширина дверных проёмов		л. 55–57	930	7 152
50	Окраска плинтуса в тоне F497, 2 слоя	м.п.	16,64		6,38	16,20	8,10	13,79	8,67	3,26	11,82		15,62	5,48		105,96	как плинтус		л. 55–57	300	31 788
51	Монтаж межкомнатных дверей (поставщик дверей)	шт	1	1	1	1	1	1	1	1	1	1		1	1	12	по ведомости проёмов		л. 22	5 250	63 000
Итого по разделу 3 — 893 133 ₽ (позиций 18); в сводную смету — л. 123, 124																					

Ведомость подсчёта площадей по помещениям

№	Помещение	S пола, м²	P, м	H, м	P × H, м²	Проёмы, м²	Стены нетто, м²	В дверных проёмах, м²	Плинтус, м	Откосы, м.п.
1	Зал	18,16	17,54	2,50	43,85	4,36	39,49	0,05	16,64	4,75
2	Ванная комната	5,57	9,47	2,52	23,82	1,47	22,35	0,04	нет	нет
3	Тёмная комната	2,96	7,08	2,60	18,41	1,47	16,94	0,04	6,38	нет
4	Детская 1	17,51	17,10	2,60	44,46	4,34	40,12	0,05	16,20	4,73
5	Коридор	4,54	10,40	2,60	27,04	4,83	22,21	0,14	8,10	нет
6	Кухня	15,19	15,59	2,60	40,53	4,95	35,59	0,11	13,79	3,93
7	Прихожая-коридор	7,80	11,17	2,60	29,05	5,25	23,80	0,15	8,67	нет
8	Гардеробная 2	1,29	4,62	2,60	12,01	3,36	8,65	0,10	3,26	нет
9	Детская 2	10,96	13,32	2,60	34,63	5,55	29,08	0,09	11,82	4,70
10	Санузел	1,31	4,66	2,52	11,72	1,26	10,46	0,04	нет	нет
11	Гостиная	14,55	17,04	2,50	42,60	5,38	37,22	0,09	15,62	4,70
12	Гардеробная 1	2,83	6,90	2,60	17,94	2,98	14,96	0,09	5,48	нет
13	Балкон 1	3,70	8,42	2,53	21,30	4,79	16,51	0,04	7,69	5,40
	Итого	**106,37**			**367,36**	**49,99**	**317,37**	**1,02**	**113,65**	**28,20**

Реестр контрольных сумм

Показатель	По ВОР	По чертежу	Расхождение	Лист
Σ площадей помещений без летних, м² — общая площадь по экспликации	102,67	102,67	0,0 %	л. 20
Стены под окраску, м² (шпаклёвка) ведомость отделки	283,46	283,45	0,0 %	л. 55–57
Потолки под окраску, м² — ведомость отделки	106,37	106,37	0,0 %	л. 55–57
Плинтус, м — ведомость отделки	113,65	113,65	0,0 %	л. 55–57
Плитка к заказу, шт — ведомость плитки	253	253	0,0 %	л. 49
Гидроизоляция, м² — ведомость материалов плитки	14,74	14,74	0,0 %	л. 49
Точки ЭОМ, шт — планы ЭОМ (без щитов)	143	147	-2,7 %	л. 29, 30

Примечания

1. Объёмы — от геометрии проекта (та же, что на планах и в ведомости отделки), не от общей площади: P — периметр чистого контура, H — от чистого пола до низа потолка, проёмы — по наружному обводу коробок.
2. Подсчёт по ГЭСН-2001-15 и ГЭСН-2001-11: штукатурка и шпаклёвка стен — за вычетом проёмов; окраска водными составами — без вычета проёмов (п. 2.24); откосы — отдельно, по ширине до 200 и более 200 мм; полы — с площадью в дверных проёмах.
3. Плитка — по раскладке (целые и с подрезкой); короб инсталляции и фартук — отдельными строками, двойного счёта облицовки нет. Материалы, запас и количество к заказу — в спецификации материалов.
4. Цены — ориентир по открытым прайсам Москвы (цены на 21.09.2026), не коммерческое предложение; «по КП» — расценки нет, строка в итог не входит.
5. Демонтаж — по плану демонтажа и общим указаниям: покрытия пола, отделка стен и потолков, дверные блоки — до основания; объёмы справочные, уточняются по факту на объекте (расценки в книге нет — «по КП»).
6. Штробы в стенах — только после технического заключения о несущих стенах (общие указания, план обмера и демонтажа): строка «Штробы в стенах» вертикальные спуски кабеля от потолочной трассы к точкам, объём не меньше фактического (горизонтальные трассы — по исполнительной схеме). Расценки штробления в прайсе нет — «по КП», в итог не входит; кабель в штробах стен прокладывается после неё.
7. Площадь облицовки стен — одно число с тремя названиями: зона облицовки по ведомости отделки 32,81 м² − место за коробом инсталляции 1,71 м² (плитку туда не кладут) = стены под плитку 31,10 м² (строка «Облицовка стен»); облицовка коробов 3,12 м² — отдельной строкой; стены и короба вместе — 34,22 м² (столько плитки по раскладке в спецификации). Источник — один (quantities.js), расхождение на листах ловит.
8. Слаботочные сети: кабель по лучам от ЩС** 85,20 м (U/UTP, RG-6, домофон — по видам), гофра 76,70 м, щит ЩС** с патч-панелью; розетки RJ45 и ТВ монтируются в строке «Электроточка». Длины те же, что в ведомости изделий электрика (одна модель — lowcurrent-engineer/bom.js); оборудование заказчика (точки доступа, камеры, коммутатор) в спецификацию не входит. 3 точ. — предложение листа слаботочки.
9. Коробы: стояков (нет) и К1 над чистым полом (6,16 м открытых участков; труба К1 вдоль стен 26,80 м в короб не зашивается — она за приборами, в раме инсталляции и в шахтах). В спецификации ВК короб К1 заказывается с запасом 10 % — 6,80 м. Материалы коробов стояков и инсталляции — в спецификации материалов, К1 — в спецификации ВК.

Допущения и предложения на листе

Основа листа: размеры сняты с размерных цепочек растрового скана плана заказчика, на объекте не замерены; ступени наружного контура приведены к граням помещений модели (ИЗ-8, К-20, К-21); высота потолка 2700 мм принята, источника нет (К-24); тип дома и перекрытие (монолит, плита 220 мм) приняты, источника нет (К-3); толщины стен приняты (250 и 120 мм), источника нет (К-21); мощность 15 кВт принята, технических условий нет (К-25).

Знак «**» — предложение проектировщика, заказчиком не утверждено (согласовать с заказчиком): ИЗ-9: ЩС — щит слаботочный: место и состав.

См. лист открытых вопросов (лист 6, запись К-3; лист 7, записи К-20, К-21, К-24, К-25; лист 10, записи ИЗ-8, ИЗ-9).

Изм.	Кол.уч	Лист	№ док.	Подп.	Дата	ГД-2026-004-АИ			
						Четырёхкомнатная квартира			
						Общая площадь 102,67* м² · * размеры со скана, не замерены (реестр — л. 6–11, ИЗ-8, К-20, К-21)			
Разраб.		Кырлан А.С.			21.10.26	Дизайн-проект интерьера четырёхкомнатной квартиры	Стадия	Лист	Листов
Пров.							РП	120	124
ГИП		Кырлан А.С.			21.10.26				
Н. контр.						Ведомость объёмов работ (окончание) М б/м	Кырлан Александр Сергеевич		
Утв.									

Спецификация материалов

Отделочные материалы: чистое количество, запас, упаковка, к заказу · ГОСТ 21.110-2013

Спецификация материалов (ГОСТ 21.110-2013, форма 1)

Поз.	Наименование и техническая характеристика	Тип, марка, артикул	Код продукции	Поставщик	Ед. изм.	Количество				Масса ед., кг	Примечание
						чистое	запас, %	упаковка	к заказу		
Покрытия полов и облицовка											
1	Инженерная доска (дуб натуральный, рабочий слой 4 мм, эмиссия E1, прямая укладка)	аналог: дуб натуральный брашированный, масло-воск, 14/4 мм			м²	84,06	7	по артикулу	90,00 м²		пом. 1, 3, 4, 6, 8, 9, 11, 12; до целой упаковки; л. 53, 55–57
2	Клей для паркетной и инженерной доски (эластичный, по ТУ изготовителя доски)	по выбору подрядчика			м²	84,06		ведро по ТУ	по ТУ		расход кг/м² — по ТУ клея; л. 53
3	Керамогранит 600,8×600,8 мм матовый R10, тон J484	керамогранит матовый R10, тон J484			шт	26	10	коробка	29 шт		6 целых + 20 с подрезкой; 6,88 м² по раскладке, к заказу 10,47 м²; пом. 2, 10; л. 49–52
4	Керамогранит 600,8×600,8 мм матовый, тон F497	аналог: керамогранит матовый, тон F497			шт	161	10	коробка	180 шт		31 целых + 130 с подрезкой; 35,33 м² по раскладке, к заказу 64,97 м²; пом. 2, 6, 10; л. 49–52
5	Керамогранит 600,8×600,8 мм матовый R10, тон V486	керамогранит матовый R10, тон V486			шт	39	10	коробка	44 шт		9 целых + 30 с подрезкой; 12,34 м² по раскладке, к заказу 15,88 м²; пом. 5, 7; л. 49–52
6	Керамогранит, R11	аналог: керамогранит матовый R11, тон V486, 600×600×10 мм			м²	3,74	10	коробка	4,20 м²		пом. 13 (пол); раскладки нет — по площади отделки; л. 55–57
Сухие смеси и гидроизоляция											
7	Клей плиточный цементный класса C2 TE S1 (ГОСТ Р 56387-2018)	аналог: Litokol K80 Eco или аналог			кг	394,31	10	мешок 25 кг	18 меш.	25	слой 5 мм, 1,50 кг/м² на 1 мм; л. 49
8	Затирка цементная класса CG2WA, цвет — по колерной карте	аналог: Mapei Ultracolor 133 или аналог			кг	5,17	10	упак. 2 кг	3 упак.	2	расход (a+b)/ab × шов × t × 1,6 кг/м²; л. 49
9	Гидроизоляция обмазочная полимерная, 2 слоя, лента в углах, манжеты на выводах	по выбору подрядчика			м²	14,74	10	ведро по ТУ	по ТУ		пом. 2, 10; расход кг/м² — по ТУ; л. 49
10	Лента демпферная по периметру пола из плитки	по выбору подрядчика			м	26,42	10	рулон	30,00 м		л. 49
11	Смесь цементно-песчаная для стяжки М200 (55 мм, 53 мм)	по выбору подрядчика			м³	5,29	5	мешок по ТУ	по ТУ		S 96,70 м² × толщина; армирование и маяки — по ТУ; л. 53
12	Смесь штукатурная гипсовая для машинного и ручного нанесения по маякам, слой до 10 мм	по выбору подрядчика			м²	317,38	10	мешок по ТУ	по ТУ		пом. 1, 2, 3, 4, 5, 6, 7, 8, 9, 10, 11, 12, 13; расход кг/м² на 1 мм слоя — по ТУ смеси, толщина — по замеру кривизны стен; л. 20, 55–57
Короба из ГКЛВ											
13	Лист ГКЛВ 12,5 мм, 2500 × 1200 мм, обшивка коробов в 2 слоя	по выбору подрядчика			м²	6,24	10	лист 3,00 м²	3,00 лист		инсталляция пом. 2: 1,36 м²; инсталляция пом. 10: 1,76 м²; площадь × 2 слоя; короб К1 над полом — в спецификации ВК; л. 40, 49–52
14	Профиль стальной оцинкованный 27 × 28 мм: каркас коробов (стойки и направляющие)	по выбору подрядчика			м	15,17	10	хлыст 3 м	6 шт		стойки через 400 мм по свободному периметру + направляющие по полу и потолку; крепёж, лента, шпаклёвка швов — по узлу короба; л. 40, 49–52
Слаботочные сети											
15	Кабель коаксиальный RG-6 (75 Ом) к розеткам ТВ	по выбору подрядчика			м	14,50		бухта по ТУ	15,00 м		по лучам от ЩС**, 1 точ., запас 10 % уже в длине; 3 точ. — предложение листа слаботочки (знак «*» на плане); л. 37
16	Кабель U/UTP кат. 6 (LAN, Wi-Fi и камеры по PoE)	по выбору подрядчика			м	70,70		бухта по ТУ	71,00 м		по лучам от ЩС**, 6 точ., запас 10 % уже в длине; 3 точ. — предложение листа слаботочки (знак «*» на плане); л. 37
17	Гофротруба Ø20 для слаботочных линий, отдельно от силовых	по выбору подрядчика			м	76,70		бухта по ТУ	77,00 м		по длине лучей без участков в канале плинтуса (≈ 90 %); л. 37
18	Розетка компьютерная RJ45, кат. 6, с рамкой и подрозетником	по выбору подрядчика			шт	4		шт	4 шт		LAN1–LAN3, LAN4**; серия механизмов — как у розеток и выключателей; л. 32, 33, 37
19	Розетка телевизионная (коаксиальная) с рамкой и подрозетником	по выбору подрядчика			шт	1		шт	1 шт		ТВ1; серия механизмов — как у розеток и выключателей; л. 32, 33, 37
20	Щит слаботочный ЩС**: корпус, DIN-рейка, розетки 220 В	по выбору подрядчика			шт	1		шт	1 шт		ЩС**; серия механизмов — как у розеток и выключателей; л. 32, 33, 37

Допущения и предложения на листе

Основа листа: размеры сняты с размерных цепочек растрового скана плана заказчика, на объекте не замерены; ступени наружного контура приведены к граням помещений модели (ИЗ-8, К-20, К-21); высота потолка 2700 мм принята, источника нет (К-24); тип дома и перекрытие (монолит, плита 220 мм) приняты, источника нет (К-3); толщины стен приняты (250 и 120 мм), источника нет (К-21); мощность 15 кВт принята, технических условий нет (К-25).

Знак «**» — предложение проектировщика, заказчиком не утверждено (согласовать с заказчиком): ИЗ-1, К-26: пол пом. 9 — направление паркета изменено вслед за окном: по оси X → по оси Y; артикул изделия не выбран: позиция описана характеристиками («аналог по характеристикам»), артикул выбирается при закупке; ИЗ-9: ЩС — щит слаботочный: место и состав; LAN4; К-26: пол пом. 1–8, 10–13, плинтус пом. 1, 3–9, 11–13, акцент пом. 1, 11, стены пом. 2, 10, фартук пом. 6 — артикул изделия не выбран: позиция описана характеристиками («аналог по характеристикам»), артикул выбирается при закупке.

Открытые вопросы и конфликты по листу: К-26.

См. лист открытых вопросов (лист 6, запись К-3; лист 7, записи К-20, К-21, К-24, К-25; лист 8, запись К-26; лист 9, запись ИЗ-1; лист 10, записи ИЗ-8, ИЗ-9).

Изм.	Кол.уч	Лист	№ док.	Подп.	Дата
Разраб.		Кырлан А.С.			21.10.26
Пров.					
ГИП		Кырлан А.С.			21.10.26
Н. контр.					
Утв.					

ГД-2026-004-АИ

Четырёхкомнатная квартира

Общая площадь 102,67* м² · * размеры со скана, не замерены (реестр — л. 6–11, ИЗ-8, К-20, К-21)

Дизайн-проект интерьера четырёхкомнатной квартиры

Стадия	Лист	Листов
РП	121	124

Спецификация материалов

М б/м

Кырлан Александр Сергеевич

Спецификация материалов (окончание)

Отделочные материалы: чистое количество, запас, упаковка, к заказу · ГОСТ 21.110-2013

Спецификация материалов (ГОСТ 21.110-2013, форма 1) (продолжение)

Поз.	Наименование и техническая характеристика	Тип, марка, артикул	Код продукции	Поставщик	Ед. изм.	Количество				Масса ед., кг	Примечание
						чистое	запас, %	упаковка	к заказу		
21	Патч-панель, портов не менее 6	по выбору подрядчика			шт	1		шт	1 шт		серия механизмов — как у розеток и выключателей; л. 32, 33, 37
Лакокрасочные материалы											
22	Краска интерьерная акриловая, матовая, класс истирания 2	Tikkurila Optiva 5 Matt L481 «Silhouette»			л	8,73	10	банка 2,7 л	4 банк		24,25 м² × 3 сл. × 0,12 л/м²; пом. 1, 11; л. 55–57
23	Краска интерьерная акриловая, матовая, класс истирания 2	Tikkurila Optiva 5 Matt F497 «Paper»			л	22,32	10	банка 2,7 л	10 банк		93,00 м² × 2 сл. × 0,12 л/м²; пом. 1, 3, 8, 11, 12; л. 55–57
24	Краска интерьерная акриловая, глубокоматовая, класс истирания 2	Tikkurila Anti-Reflex 2 F497 «Paper»			л	19,34	10	банка 2,7 л	8 банк		80,60 м² × 2 сл. × 0,12 л/м²; пом. 1 (пот.), 3 (пот.), 4 (пот.), 5 (пот.), 7 (пот.), 8 (пот.), 9 (пот.), 11 (пот.), 12 (пот.); л. 55–57
25	Краска интерьерная акриловая, матовая, класс истирания 1	Tikkurila Luja 7 F497 «Paper»			л	6,18	10	банка 2,7 л	3 банк		25,77 м² × 2 сл. × 0,12 л/м²; пом. 2 (пот.), 6 (пот.), 10 (пот.), 13 (пот.); л. 55–57
26	Краска интерьерная акриловая, полуматовая, класс истирания 2	Tikkurila Joker F497 «Paper»			л	16,61	10	банка 2,7 л	7 банк		69,20 м² × 2 сл. × 0,12 л/м²; пом. 4, 9; л. 55–57
27	Краска интерьерная акриловая, полуматовая, класс истирания 2	Tikkurila Optiva 20 Semimatt J484 «Castle»			л	11,04	10	банка 2,7 л	5 банк		46,01 м² × 2 сл. × 0,12 л/м²; пом. 5, 7; л. 55–57
28	Краска интерьерная акриловая, полуматовая, класс истирания 1	Tikkurila Luja 7 F497 «Paper»			л	12,24	10	банка 2,7 л	5 банк		50,99 м² × 2 сл. × 0,12 л/м²; пом. 6, 13; л. 55–57
29	Шпаклёвка финишная полимерная под окраску (стены и потолки, Q3)	по выбору подрядчика			м²	389,83	10	ведро по ТУ	по ТУ		расход кг/м² на слой — по ТУ; л. 55–57
30	Грунтовка акриловая глубокого проникновения, 2 слоя	по выбору подрядчика			м²	423,75	10	канистра по ТУ	по ТУ		расход л/м² — по ТУ; л. 55–57
Погонажные изделия и потолки											
31	Плинтус напольный МДФ под покраску, h=80 мм, крепление к стене	аналог: плинтус МДФ под окраску 80×16 мм			м.п.	105,96	10	хлыст 2,4 м	49 шт		пом. 1, 3, 4, 5, 6, 7, 8, 9, 11, 12; длина хлыста — по артикулу; л. 55–57
32	Керамогранит на плинтус: полосы h=80 мм из плитки пола, кромка с запилом 45°	аналог: плинтус из керамогранита пола, подрезка 80 мм, верхняя кромка с запилом 45°			м²	0,62	15	из партии пола	0,71 м²		7,69 м.п. × 0,08 м; пом. 13; заказывать целыми плитками одной партии с полом, число плиток — по раскладке плиточника; л. 53, 55–57
33	Потолок подвесной ГКЛ/ГКЛВ по каркасу Knauf П113: листы, профили, подвесы, лента, шпаклёвка швов	Knauf П113			м²	106,37		комплект	по л. потолков		площадь — по ведомости потолков; число листов, профилей и подвесов — по шагам каркаса на листе потолков; л. 44–48
Инженерные изделия											
34	Мат нагревательный электрический для тёплого пола под плитку, с холодным концом и муфтой	по выбору подрядчика (мощность — по контурам)			м²	1,67		мат по контуру	по контурам		пом. 2: 1,37 м², 205 Вт; пом. 10: 0,30 м², 50 Вт; типоразмер мата подбирается под контур — нагревательную жилу резать нельзя; л. 29, 53
35	Терморегулятор тёплого пола с выносным датчиком пола, монтаж в подрозетник	по выбору подрядчика			шт	2		шт	2 шт		датчик — в гофротрубе с доступом для замены; по одному на контур; л. 29

Примечания

1. Чистое количество — из ведомости объёмов работ и раскладки плитки; запас — отдельной графой (доска — по ведомости отделки, плитка, краска и плинтус — 10 %); «к заказу» — с запасом и кратно упаковке.
2. Плитка — штуками по раскладке, запас на каждую поверхность. Калибр (рабочий размер) и тон — одной партией на помещение, калибр указать при заказе и сверить с раскладкой до укладки.
3. Краска — 0,12 л/м² на слой (середина вилки 0,10–0,15 л/м²) по фактической площади окраски из ведомости отделки; колеровка одной партией.
4. «По ТУ» — расход задаёт производитель выбранного продукта; количество к заказу — после выбора марки.
5. Поз. 1, 4, 6, 31, 32 заданы характеристиками («аналог:»): марку, артикул и поставщика согласовать с заказчиком до закупки, без артикула не заказывать.
6. Штукатурная смесь — на ту же площадь, что строка ВОР «Штукатурка стен» (317,38 м²): площадь одна, расход смеси задаёт производитель.
7. Коробы инсталляции и стояков: ГКЛВ в 2 слоя и профиль 27 × 28 мм считаются по свободным граням коробов (источник — раскладка плиточника и шахты в данных); короб К1 над полом — в спецификации ВК.
8. Потолки ГКЛ: в этой спецификации — площадь системы П113; число листов, профилей и подвесов — по шагам каркаса на листе потолков (подвесы через 1000, несущие через 500, основные через 1200 мм), схема каркаса не выпущена. Сантехника, светильники и мебель — по своим спецификациям.

Допущения и предложения на листе

Основа листа: размеры сняты с размерных цепочек растрового скана плана заказчика, на объекте не замерены; ступени наружного контура приведены к граням помещений модели (ИЗ-8, К-20, К-21); высота потолка 2700 мм принята, источника нет (К-24); тип дома и перекрытие (монолит, плита 220 мм) приняты, источника нет (К-3); толщины стен приняты (250 и 120 мм), источника нет (К-21); мощность 15 кВт принята, технических условий нет (К-25).

Знак «**» — предложение проектировщика, заказчиком не утверждено (согласовать с заказчиком): ИЗ-1, К-26: пол пом. 9 — направление паркета изменено вслед за окном: по оси X → по оси Y; артикул изделия не выбран: позиция описана характеристиками («аналог по характеристикам»), артикул выбирается при закупке; К-26: пол пом. 1–8, 10–13, плинтус пом. 1, 3–9, 11–13, акцент пом. 1, 11, стены пом. 2, 10, фартук пом. 6 — артикул изделия не выбран: позиция описана характеристиками («аналог по характеристикам»), артикул выбирается при закупке.

Открытые вопросы и конфликты по листу: К-26.

См. лист открытых вопросов (лист 6, запись К-3; лист 7, записи К-20, К-21, К-24, К-25; лист 8, запись К-26; лист 9, запись ИЗ-1; лист 10, запись ИЗ-8).

Изм.	Кол.уч	Лист	№ док.	Подп.	Дата
Разраб.		Кырлан А.С.			21.10.26
Пров.					
ГИП		Кырлан А.С.			21.10.26
Н. контр.					
Утв.					

ГД-2026-004-АИ

Четырёхкомнатная квартира

Общая площадь 102,67* м² · * размеры со скана, не замерены (реестр — л. 6–11, ИЗ-8, К-20, К-21)

Дизайн-проект интерьера четырёхкомнатной квартиры

Стадия	Лист	Листов
РП	122	124

Спецификация материалов (окончание)

М б/м

Кырлан Александр Сергеевич

Смета ориентировочная

ПРЕДВАРИТЕЛЬНО · не для производства работ · открыто пунктов: 30 (реестр — л. 6–11)

Работы, материалы, оборудование, услуги и резерв · цены — ориентир по открытым прайсам, не коммерческое предложение

Сводная смета (цены на 21.09.2026, Москва)

№	Наименование работ, материалов, услуг	Ед. изм.	Кол-во	Цена за ед., ₽	Стоимость, ₽			Чей подряд	Срок поставки, дн.	Основание	Источник цены
					план	факт	разница				
Работы — по ведомости объёмов работ											
1	Демонтаж и черновые работы (без 5 поз. по КП)	раздел	1		388 064			бригада		ВОР, поз. 1–10; л. 118–120	по ВОР
2	Инженерные системы (без 10 поз. по КП)	раздел	1		192 651			бригада		ВОР, поз. 11–33; л. 118–120	по ВОР
3	Чистовые работы	раздел	1		893 133			бригада, поставщик		ВОР, поз. 34–51; л. 118–120	по ВОР
Материалы — по спецификации материалов											
4	Инженерная доска	м²	90,00	4 513	406 170			поставщик		спецификация, поз. 1	Ц7
5	Керамогранит 600,8×600,8 мм	м²	95,52	1 800	171 936			поставщик		спецификация, поз. 3, 4, 5, 6	Ц6
6	Клей плиточный цементный класса C2 TE S1	меш.	18	1 800	32 400			поставщик		спецификация, поз. 7	Ц7
7	Затирка цементная класса CG2WA	упак.	3	1 000	3 000			поставщик		спецификация, поз. 8	Ц7
8	Краска Tikkurila (Optiva 5 Matt, Anti-Reflex 2, Luja 7, Joker, Optiva 20 Semimatt), банка 2,7 л	банк	42	3 510	147 420			поставщик		спецификация, поз. 22, 23, 24, 25, 26, 27, 28	Ц6
9	Плинтус напольный МДФ под покраску	шт	49	368	18 032			поставщик		спецификация, поз. 31	Ц7
10	Керамогранит на плинтус: полосы h=80 мм из плитки пола	м²	0,71	1 800	1 278			поставщик		спецификация, поз. 32	Ц6
11	Прочие материалы с расходом по ТУ (клей для доски, гидроизоляция, демпферная лента, смесь для стяжки, смесь штукатурная гипсовая для машинного и ручного нанесения по маякам, лист гклв 12, профиль стальной оцинкованный 27 × 28 мм: каркас коробов (стойки и направляющие), кабель слаботочки, гофра слаботочки, изделия слаботочки, шпаклёвка, грунтовка, каркас и ГКЛ потолков, мат нагревательный электрический для тёплого пола под плитку, терморегулятор тёплого пола с выносным датчиком пола)	компл	1	по КП				поставщик		спецификация, поз. 2, 9, 10, 11, 12, 13, 14, 15, 16, 17, 18, 19, 20, 21, 29, 30, 33, 34, 35	
Оборудование и мебель — поставка по спецификациям											
12	Кухонный гарнитур по проекту кухни, изготовление и монтаж (4–8 нед.)	компл	1	по КП				поставщик	уточн.; ориентир 4–8 нед. от замера	л. 81–84	

Допущения и предложения на листе

Основа листа: размеры сняты с размерных цепочек растрового скана плана заказчика, на объекте не замерены; ступени наружного контура приведены к граням помещений модели (ИЗ-8, К-20, К-21); высота потолка 2700 мм принята, источника нет (К-24); тип дома и перекрытие (монолит, плита 220 мм) приняты, источника нет (К-3); толщины стен приняты (250 и 120 мм), источника нет (К-21); мощность 15 кВт принята, технических условий нет (К-25).

Открытые вопросы и конфликты по листу: К-26.

См. лист открытых вопросов (лист 6, запись К-3; лист 7, записи К-20, К-21, К-24, К-25; лист 8, запись К-26; лист 10, запись ИЗ-8).

Изм.	Кол.уч	Лист	№ док.	Подп.	Дата
Разраб.		Кырлан А.С.			21.10.26
Пров.					
ГИП		Кырлан А.С.			21.10.26
Н. контр.					
Утв.					

ГД-2026-004-АИ

Четырёхкомнатная квартира

Общая площадь 102,67* м² · * размеры со скана, не замерены (реестр — л. 6–11, ИЗ-8, К-20, К-21)

Дизайн-проект интерьера четырёхкомнатной квартиры

Стадия	Лист	Листов
РП	123	124

Смета ориентировочная

М б/м

Кырлан Александр Сергеевич

выпуск 05.10.2026 № 7e7a2cd217 · стр. 135 из 168

Смета ориентировочная (окончание)

Работы, материалы, оборудование, услуги и резерв · цены — ориентир по открытым прайсам, не коммерческое предложение

Сводная смета (цены на 21.09.2026, Москва) (продолжение)

№	Наименование работ, материалов, услуг	Ед. изм.	Кол-во	Цена за ед., ₽	Стоимость, ₽			Чей подряд	Срок поставки, дн.	Основание	Источник цены
					план	факт	разница				
13	Двери межкомнатные, поставка	шт	12	по КП				поставщик		л. 22	
14	Оборудование заказчика слаботочных сетей: точка доступа wi-fi — 2 шт; коммутатор — 1 шт	компл	1	по КП				заказчик		л. 32, 33	
15	Сантехника, светильники, мебель и предметы интерьера	компл	1	по КП				поставщик		л. 42; л. 43; л. 88; л. 25–28	
Прочие работы и услуги											
16	Вынос и вывоз строительного мусора	м³		по факту				бригада		после демонтажа	
17	Подъём материалов на этаж (лифтом или вручную — по договору)	т		по факту				бригада		по массе поставки	
18	Доставка чистовых материалов, 10 % от поставки			10 %	78 024			поставщик		от суммы материалов	
19	Уборка после ремонта	м²	102,67	по факту				бригада		S квартиры	
	Итого работы				**1 473 848**						
	Итого материалы				**780 236**						
	Итого прочие услуги				**78 024**						
	Резерв на непредвиденные работы и материалы, 15 %				**349 816**						
	ВСЕГО ориентировочно (без оборудования и позиций по КП)				**2 681 924**						

Примечания

1. Смета ориентировочная, не коммерческое предложение: объёмы — из ведомости объёмов работ и спецификации материалов, цены — нижняя граница открытых прайсов Москвы (цены на 21.09.2026); перед договором цены подтвердить у подрядчика и поставщиков.
2. Источники цен: Ц1 — Домашний мастерок: прайс на отделочные работы, 2026; Ц2 — Домашний мастерок: прайс на плиточные работы, 2026; Ц3 Домашний мастерок: прайс на электромонтажные работы, 2026; Ц4 — Профи ремонтник: штукатурно-малярные работы; Ц5 — Profi.ru: укладка керамогранита на стены, Москва 2026; Ц6 — knowledge/spec-materials.md, разд. 1 и 3: ориентир по сегментам; Ц7 — Розница Москвы, 09.2026: Лемана ПРО, KGSnab, официальный дилер Farrow & Ball.
3. В итог не вошли позиции «по КП» и «по факту»: оборудование и мебель, двери, материалы с расходом по ТУ, вывоз мусора, подъём и уборка.
4. Доставка — 10 % от материалов, резерв — 15 % (частный ремонт 10–20 %) отдельными строками, в количествах не спрятаны. Графы «факт» и «разница» заполняются по актам.

Допущения и предложения на листе

Основа листа: размеры сняты с размерных цепочек растрового скана плана заказчика, на объекте не замерены; ступени наружного контура приведены к граням помещений модели (ИЗ-8, К-20, К-21); высота потолка 2700 мм принята, источника нет (К-24); тип дома и перекрытие (монолит, плита 220 мм) приняты, источника нет (К-3); толщины стен приняты (250 и 120 мм), источника нет (К-21); мощность 15 кВт принята, технических условий нет (К-25).

Открытые вопросы и конфликты по листу: К-26.

См. лист открытых вопросов (лист 6, запись К-3; лист 7, записи К-20, К-21, К-24, К-25; лист 8, запись К-26; лист 10, запись ИЗ-8).

Изм.	Кол.уч	Лист	№ док.	Подп.	Дата
Разраб.		Кырлан А.С.			21.10.26
Пров.					
ГИП		Кырлан А.С.			21.10.26
Н. контр.					
Утв.					

ГД-2026-004-АИ

Четырёхкомнатная квартира

Общая площадь 102,67* м² · * размеры со скана, не замерены (реестр — л. 6–11, ИЗ-8, К-20, К-21)

Дизайн-проект интерьера четырёхкомнатной квартиры

Стадия	Лист	Листов
РП	124	124

Смета ориентировочная (окончание)

М б/м

Кырлан Александр Сергеевич

11

Визуализации

Кырлан Александр Сергеевич

выпуск 05.10.2026 · 7e7a2cd217 · стр. 137 из 168

Планировочное решение · вид сверху

Четырёхкомнатная квартира · визуализация 1 из 31

выпуск 05.10.2026 № 7e7a2cd217 · стр. 138 из 168

Потолок · гостиная

выпуск 05.10.2026 № 7e7a2cd217 · стр. 139 из 168

Потолок · кухня

Четырёхкомнатная квартира · визуализация 3 из 31

выпуск 05.10.2026 № 7e7a2cd217 · стр. 140 из 168

Потолок · детская 1

выпуск 05.10.2026 № 7e7a2cd217 · стр. 141 из 168

Потолок · детская 2

выпуск 05.10.2026 № 7e7a2cd217 · стр. 142 из 168

выпуск 05.10.2026 № 7e7a2cd217 · стр. 143 из 168

Потолок · прихожая

Потолок · ванная

выпуск 05.10.2026 № 7e7a2cd217 · стр. 144 из 168

Потолок · санузел

выпуск 05.10.2026 № 7e7a2cd217 · стр. 145 из 168

Потолок · гардеробная

выпуск 05.10.2026 № 7e7a2cd217 · стр. 146 из 168

Потолок · кладовая

выпуск 05.10.2026 № 7e7a2cd217 · стр. 147 из 168

Потолок · балкон

Четырёхкомнатная квартира · визуализация 11 из 31

выпуск 05.10.2026 № 7e7a2cd217 · стр. 148 из 168

room-balcony-wD

room-bath-wB

Четырёхкомнатная квартира · визуализация 13 из 31

выпуск 05.10.2026 № 7e7a2cd217 · стр. 150 из 168

room-corridor-wA

Четырёхкомнатная квартира · визуализация 14 из 31

выпуск 05.10.2026 № 7e7a2cd217 · стр. 151 из 168

room-corridor-wC

выпуск 05.10.2026 № 7e7a2cd217 · стр. 152 из 168

room-hall-wide

Четырёхкомнатная квартира · визуализация 16 из 31

выпуск 05.10.2026 № 7e7a2cd217 · стр. 153 из 168

room-kids1-wC

выпуск 05.10.2026 № 7e7a2cd217 · стр. 154 из 168

room-kids1-wD

Четырёхкомнатная квартира · визуализация 18 из 31

выпуск 05.10.2026 № 7e7a2cd217 · стр. 155 из 168

room-kids2-wA

Четырёхкомнатная квартира · визуализация 19 из 31

выпуск 05.10.2026 № 7e7a2cd217 · стр. 156 из 168

выпуск 05.10.2026 № 7e7a2cd217 · стр. 157 из 168

room-kids2-wD

выпуск 05.10.2026 № 7e7a2cd217 · стр. 158 из 168

room-kitchen-wA

room-living1-wA

Четырёхкомнатная квартира · визуализация 22 из 31

выпуск 05.10.2026 № 7e7a2cd217 · стр. 159 из 168

выпуск 05.10.2026 № 7e7a2cd217 · стр. 160 из 168

room-living1-wB

room-living1-wC

Четырёхкомнатная квартира · визуализация 24 из 31

выпуск 05.10.2026 № 7e7a2cd217 · стр. 161 из 168

выпуск 05.10.2026 № 7e7a2cd217 · стр. 162 из 168

room-living1-wD

room-living2-wA

Четырёхкомнатная квартира · визуализация 26 из 31

выпуск 05.10.2026 № 7e7a2cd217 · стр. 163 из 168

room-living2-wB

выпуск 05.10.2026 № 7e7a2cd217 · стр. 164 из 168

room-storage-wide

Четырёхкомнатная квартира · визуализация 28 из 31

выпуск 05.10.2026 № 7e7a2cd217 · стр. 165 из 168

room-wardrobe1-wide

выпуск 05.10.2026 № 7e7a2cd217 · стр. 166 из 168

room-wardrobe2-wide

выпуск 05.10.2026 № 7e7a2cd217 · стр. 167 из 168

room-wc-wide

выпуск 05.10.2026 № 7e7a2cd217 · стр. 168 из 168