
LINEA

ДИЗАЙН-ПРОЕКТ ИНТЕРЬЕРА

Дом 147 м²

Средиземноморский

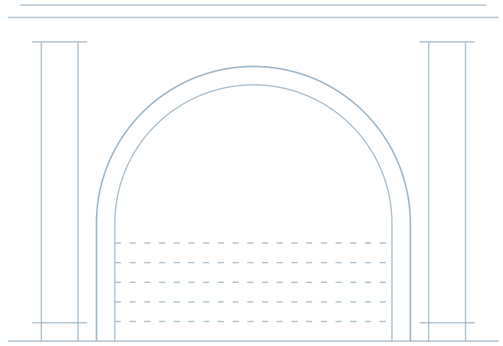

ПАЛИТРА ОТДЕЛКИ

G503	Little Greene	NCS S 0502-Y	NCS S 5020-G90	NCS S 3050-R80
53 %	33 %	5 %	2 %	2 %

АВТОР ПРОЕКТА

Кырлан Александр Сергеевич

Ноябрь 2026



Квартира сверху · схематичная модель по плану

ОБЩАЯ ПЛОЩАДЬ	ПОМЕЩЕНИЙ	СТАДИЯ	ШИФР	ОСНОВА
147,36 м²	13, из них жилых 5	Рабочий проект · предварительно	ГД-2026-012-АИ	план заказчика, без обмера

Изм.	Кол.уч	Лист	№ док.	Подп.	Дата
Разраб.		Кырлан А.С.			04.11.26
Пров.					
ГИП					
Н. контр.					
Утв.					

ГД-2026-012-АИ

Дом 120 м²

Общая площадь 147,36* м² · * размеры приняты, не замерены (реестр — л. 7–9, К-1)

Дизайн-проект интерьера

Стадия	Лист	Листов
РП	1	175

Титульный лист

М б/м

Кырлан Александр Сергеевич

выпуск 04.11.2026 № 4dfa962484 · стр. 1 из 180

Общие данные

ПРЕДВАРИТЕЛЬНО · не для производства работ · открыто пунктов: 11 (реестр — л. 7–9)

Комплект ГД-2026-012-АИ · Дом 120 м² в два этажа (демо LINEA)

Допущения и предложения на листе. См. лист открытых вопросов (листы 7–9).

Ведомость рабочих чертежей основного комплекта ГД-2026-012-АИ

Лист	Наименование	Примечание
1	Титульный лист	
2	Общие данные	
3	Общие данные	
4	Общие данные	
5	Общие данные	
6	Общие данные	
7	Открытые вопросы, принятые допущения и конфликты. Лист 1 из 3	
8	Открытые вопросы, принятые допущения и конфликты. Лист 2 из 3	
9	Открытые вопросы, принятые допущения и конфликты. Лист 3 из 3	
10	Задание на контрольный обмер и обследование. Лист 1 из 4	
11	Задание на контрольный обмер и обследование. Лист 2 из 4	
12	Задание на контрольный обмер и обследование. Лист 3 из 4	
13	Задание на контрольный обмер и обследование. Лист 4 из 4	
14	График закупок и работ. Лист 1 из 3	
15	График закупок и работ. Лист 2 из 3	
16	График закупок и работ. Лист 3 из 3	
17	Обмерный план · 1-й этаж	
18	Обмерный план · 2-й этаж	
19	План демонтажа и монтажа перегородок · 1-й этаж	
20	План демонтажа и монтажа перегородок · 2-й этаж	
21	План дверей · 1-й этаж	
22	План дверей · 2-й этаж	
23	Ведомость заполнения проёмов	
24	Лестница Л-1	
25	Концепция интерьера · 1-й этаж	
26	Концепция интерьера · 2-й этаж	
27	План расстановки мебели · 1-й этаж	
28	План расстановки мебели · 2-й этаж	
29	Спецификация мебели и оборудования	
30	Спецификация мебели и оборудования (продолжение)	

Ведомость рабочих чертежей основного комплекта ГД-2026-012-АИ (продолжение)

Лист	Наименование	Примечание
31	Спецификация мебели и оборудования (продолжение)	
32	Спецификация мебели и оборудования (продолжение)	
33	Спецификация мебели и оборудования (продолжение)	
34	План розеток и электровыводов · 1-й этаж	
35	План розеток и электровыводов · 2-й этаж	
36	План освещения · 1-й этаж	
37	План освещения · 2-й этаж	
38	План выключателей и схема включения · 1-й этаж	
39	План выключателей и схема включения · 2-й этаж	
40	Ведомость электроточек и изделий	
41	Ведомость электроточек и изделий (продолжение)	
42	Однолинейная схема щита	
43	Однолинейная схема щита (продолжение)	
44	План принципиальных трасс · 1-й этаж	
45	План принципиальных трасс · 2-й этаж	
46	План слаботочных сетей · 1-й этаж	
47	План слаботочных сетей · 2-й этаж	
48	План вентиляции · 1-й этаж	
49	План вентиляции · 2-й этаж	
50	План отопления · 1-й этаж	
51	План отопления · 2-й этаж	
52	План выводов сантехники · 1-й этаж	
53	План выводов сантехники · 2-й этаж	

Общие указания — лист 6: ±0,000 — чистый пол 1-го этажа; несущие конструкции и сети — по отдельному проекту; скрытые работы — по актам. Вопросы и допущения — листы 7–9.

Изм.	Кол.уч	Лист	№ док.	Подп.	Дата
Разраб.		Кырлан А.С.			04.11.26
Пров.					
ГИП					
Н. контр.					
Утв.					

ГД-2026-012-АИ

Дом 120 м²

Общая площадь 147,36* м² · * размеры приняты, не замерены (реестр — л. 7–9, К-1)

Дизайн-проект интерьера

Стадия	Лист	Листов
РП	2	175

Общие данные

М б/м

Кырлан Александр Сергеевич

выпуск 04.11.2026 № 4dfa962484 · стр. 2 из 180

Общие данные

Комплект ГД-2026-012-АИ · лист 2 общих данных (продолжение)

Допущения и предложения на листе. См. лист открытых вопросов (листы 7–9).

Ведомость рабочих чертежей основного комплекта ГД-2026-012-АИ (продолжение)

Лист	Наименование	Примечание
54	Схема разводки водопровода и канализации · 1-й этаж	
55	Схема разводки водопровода и канализации · 2-й этаж	
56	Аксонометрическая схема В1 (холодное водоснабжение)	
57	Аксонометрическая схема Т3 (горячее водоснабжение)	
58	Аксонометрическая схема К1 (канализация)	
59	Развёртки мокрых зон: выводы ВК. Гостиная-кухня	
60	Развёртки мокрых зон: выводы ВК. Санузел гостевой	
61	Развёртки мокрых зон: выводы ВК. Санузел второго этажа (лист 1 из 2)	
62	Развёртки мокрых зон: выводы ВК. Санузел второго этажа (лист 2 из 2)	
63	Спецификация сантехнического оборудования	
64	Техническое задание на подбор светильников	
65	Техническое задание на подбор светильников (продолжение)	
66	План потолков · 1-й этаж	
67	План потолков · 2-й этаж	
68	Разрезы и узлы потолков	
69	Разрезы и узлы потолков (продолжение)	
70	Разрезы и узлы потолков (продолжение)	
71	Разрезы и узлы потолков (продолжение)	
72	Сечения потолков М 1:10	
73	Сечения потолков М 1:10	
74	Раскладка плитки. Планы полов	
75	Раскладка плитки. Прихожая. Фартук кухни	
76	Раскладка плитки. Санузел гостевой. Развёртки стен	
77	Раскладка плитки. Санузел второго этажа. Развёртки стен	
78	План полов · 1-й этаж	
79	План полов · 2-й этаж	
80	Ведомость отделки помещений. Лист 1 из 3	
81	Ведомость отделки помещений. Лист 2 из 3	
82	Ведомость отделки помещений. Лист 3 из 3	
83	Колерная карта · 1-й этаж	

Ведомость рабочих чертежей основного комплекта ГД-2026-012-АИ (продолжение)

Лист	Наименование	Примечание
84	Колерная карта · 2-й этаж	
85	Колерная карта	
86	Спецификация отделочных материалов	
87	Спецификация отделочных материалов	
88	Концепция декора и визуализации	
89	План текстиля и декора · 1-й этаж	
90	План текстиля и декора · 2-й этаж	
91	Шторы и карнизы	
92	Ведомость текстиля	
93	Ведомость текстиля (продолжение)	
94	Ведомость декора. Схемы развески	
95	Схемы развески (продолжение)	
96	Встроенная мебель. Схема расположения · 1-й этаж	
97	Встроенная мебель. Схема расположения · 2-й этаж	
98	Шкаф-купе Пх1	
99	Шкаф распашной М4	
100	Шкаф распашной Дт3	
101	Система хранения Гд1	
102	Система хранения Гд2	
103	Система хранения Кл1	
104	Система хранения Кл2	
105	Шкаф распашной Дт8	
106	Система хранения Дт10	

Общие указания — лист 6: ±0,000 — чистый пол 1-го этажа; несущие конструкции и сети — по отдельному проекту; скрытые работы — по актам. Вопросы и допущения — листы 7–9.

Изм.	Кол.уч	Лист	№ док.	Подп.	Дата	ГД-2026-012-АИ		
						Дом 120 м²		
						Общая площадь 147,36* м² · * размеры приняты, не замерены (реестр — л. 7–9, К-1)		
Разраб.		Кырлан А.С.			04.11.26	Дизайн-проект интерьера	Стадия	Лист	Листов
Пров.							РП	3	175
ГИП									
						Общие данные	Кырлан Александр Сергеевич		
Н. контр.						М б/м			
Утв.									

выпуск 04.11.2026 № 4dfa962484 · стр. 3 из 180

Общие данные

ПРЕДВАРИТЕЛЬНО · не для производства работ · открыто пунктов: 11 (реестр — л. 7–9)

Допущения и предложения на листе. См. лист открытых вопросов (листы 7–9).

Ведомость рабочих чертежей основного комплекта ГД-2026-012-АИ (продолжение)

Лист	Наименование	Примечание
107	Кухня (пом. 1). Развёртка гарнитура	
108	Кухня (пом. 1). Монтажная схема	
109	Кухня (пом. 1). Развёртка гарнитура	
110	Кухня (пом. 1). Монтажная схема	
111	Шкафы. Монтажная схема. Лист 1 из 2	
112	Шкафы. Монтажная схема. Лист 2 из 2	
113	Ведомости изделий, техники и фурнитуры	
114	Реестр марок отделки и позиций альбома	
115	Реестр марок отделки и позиций альбома (продолжение)	
116	Схема расположения развёрток и узлов · 1-й этаж	
117	Схема расположения развёрток и узлов · 2-й этаж	
118	Развёртка стены А. Гостиная-кухня (пом. 1), кухонный фронт	
119	Привязки электроточек и выводов ВК, стена А. Гостиная-кухня (пом. 1)	
120	Развёртка стены А: схема и ведомость отделки. Гостиная-кухня (пом. 1)	
121	Развёртка стены Б. Гостиная-кухня (пом. 1), кухонный фронт	
122	Привязки электроточек, стена Б. Гостиная-кухня (пом. 1)	
123	Развёртка стены В. Гостиная-кухня (пом. 1)	
124	Привязки электроточек, стена В. Гостиная-кухня (пом. 1)	
125	Развёртка стены В: схема и ведомость отделки. Гостиная-кухня (пом. 1)	
126	Развёртка стены Г. Гостиная-кухня (пом. 1)	
127	Развёртка стены А. Холл с лестницей (пом. 2)	
128	Развёртка стены В. Холл с лестницей (пом. 2)	
129	Развёртка стены Г. Холл с лестницей (пом. 2)	
130	Развёртка стены А. Кабинет (пом. 3)	
131	Развёртка стены Б. Кабинет (пом. 3)	
132	Развёртка стены В. Кабинет (пом. 3)	
133	Развёртка стены Г. Кабинет (пом. 3)	
134	Развёртки стен А, Б. Санузел гостевой (пом. 4)	
135	Привязки электроточек и выводов ВК, стена А. Санузел гостевой (пом. 4)	

Ведомость рабочих чертежей основного комплекта ГД-2026-012-АИ (продолжение)

Лист	Наименование	Примечание
136	Развёртки стен В, Г. Санузел гостевой (пом. 4)	
137	Развёртка стены А1. Прихожая (пом. 5)	
138	Развёртка стены А2. Прихожая (пом. 5)	
139	Развёртка стены Б. Прихожая (пом. 5)	
140	Развёртка стены В. Прихожая (пом. 5)	
141	Развёртка стены В: схема и ведомость отделки. Прихожая (пом. 5)	
142	Развёртки стен Г1, Г2. Прихожая (пом. 5)	
143	Развёртка стены А. Спальня родителей (пом. 6)	
144	Развёртка стены Б. Спальня родителей (пом. 6)	
145	Развёртка стены В. Спальня родителей (пом. 6)	
146	Развёртка стены Г. Спальня родителей (пом. 6)	
147	Привязки электроточек, стена Г. Спальня родителей (пом. 6)	
148	Развёртка стены А. Детская (пом. 7)	
149	Развёртка стены Б. Детская (пом. 7)	
150	Развёртка стены В. Детская (пом. 7)	
151	Развёртка стены Г. Детская (пом. 7)	
152	Развёртки стен А, Б. Гардеробная (пом. 8)	
153	Развёртки стен В, Г. Гардеробная (пом. 8)	
154	Развёртки стен. Кладовая (пом. 9)	
155	Развёртка стены А. Холл второго этажа (пом. 10)	
156	Развёртка стены В. Холл второго этажа (пом. 10)	
157	Развёртка стены Г. Холл второго этажа (пом. 10)	
158	Развёртки стен А, В. Коридор второго этажа (пом. 11)	

Общие указания — лист 6: ±0,000 — чистый пол 1-го этажа; несущие конструкции и сети — по отдельному проекту; скрытые работы — по актам. Вопросы и допущения — листы 7–9.

Изм.	Кол.уч	Лист	№ док.	Подп.	Дата	ГД-2026-012-АИ			
						Дом 120 м²			
						Общая площадь 147,36* м² · * размеры приняты, не замерены (реестр — л. 7–9, К-1)			
Разраб.		Кырлан А.С.			04.11.26	Дизайн-проект интерьера	Стадия	Лист	Листов
Пров.							РП	4	175
ГИП						Общие данные	Кырлан Александр Сергеевич		
						М б/м			
Н. контр.									
Утв.									

выпуск 04.11.2026 № 4dfa962484 · стр. 4 из 180

Общие данные

Комплект ГД-2026-012-АИ · лист 4 общих данных (продолжение)

Ведомость рабочих чертежей основного комплекта ГД-2026-012-АИ (продолжение)

Лист	Наименование	Примечание
159	Развёртка стены Г. Коридор второго этажа (пом. 11)	
160	Развёртка стены А. Детская вторая (пом. 12)	
161	Развёртка стены Б. Детская вторая (пом. 12)	
162	Развёртка стены В. Детская вторая (пом. 12)	
163	Развёртка стены Г. Детская вторая (пом. 12)	
164	Развёртки стен А, Б. Санузел второго этажа (пом. 13)	
165	Привязки электроточек и выводов ВК, стена А. Санузел второго этажа (пом. 13)	
166	Привязки электроточек и выводов ВК, стена Б. Санузел второго этажа (пом. 13)	
167	Развёртки стен В, Г. Санузел второго этажа (пом. 13)	
168	Узлы	
169	Ведомость объёмов работ	
170	Ведомость объёмов работ (продолжение)	
171	Ведомость объёмов работ (окончание)	
172	Спецификация материалов	
173	Спецификация материалов (окончание)	
174	Смета ориентировочная	
175	Смета ориентировочная (окончание)	

Ведомость ссылочных и прилагаемых документов

Обозначение	Наименование	Примечание
	Ссылочные документы	
ГОСТ 21.201-2011	СПДС. Условные графические изображения элементов зданий, сооружений и конструкций	
ГОСТ 21.205-2016	СПДС. Условные обозначения элементов санитарно-технических систем	
ГОСТ 21.210-2014	СПДС. Изображения условные графические электрооборудования и проводок на планах	
ГОСТ 2.306-68	ЕСКД. Обозначения графические материалов и правила их нанесения на чертежах	
	Прилагаемые документы	
ГД-2026-012-АИ.В1	Визуализация. Вид сверху (3D): планировка с мебелью, текстилем и декором	альбом визуализаций
ГД-2026-012-АИ.В2	Визуализация. Вид сверху (3D): планировка с мебелью, текстилем и декором	
ГД-2026-012-АИ.В3	Визуализация. Интерьер: Санузел второго этажа (пом. 13), общий вид	
ГД-2026-012-АИ.В4	Визуализация. Интерьер: Спальня родителей (пом. 6), стена В	
ГД-2026-012-АИ.В5	Визуализация. Интерьер: Спальня родителей (пом. 6), стена Г	
ГД-2026-012-АИ.В6	Визуализация. Интерьер: Холл с лестницей (пом. 2), стена Б	
ГД-2026-012-АИ.В7	Визуализация. Интерьер: Холл второго этажа (пом. 10), общий вид	
ГД-2026-012-АИ.В8	Визуализация. Интерьер: Коридор второго этажа (пом. 11), общий вид	
ГД-2026-012-АИ.В9	Визуализация. Интерьер: Прихожая (пом. 5), стена А	
ГД-2026-012-АИ.В10	Визуализация. Интерьер: Прихожая (пом. 5), стена Б	
ГД-2026-012-АИ.В11	Визуализация. Интерьер: Детская (пом. 7), стена А	
ГД-2026-012-АИ.В12	Визуализация. Интерьер: Детская (пом. 7), стена В	
ГД-2026-012-АИ.В13	Визуализация. Интерьер: Детская вторая (пом. 12), стена А	
ГД-2026-012-АИ.В14	Визуализация. Интерьер: Детская вторая (пом. 12), стена Г	
ГД-2026-012-АИ.В15	Визуализация. Интерьер: Гостиная-кухня (пом. 1), стена А	

Допущения и предложения на листе

Основа листа: взаимное расположение помещений, контур дома 9600 × 8000 и раскладка этажей подобраны проектировщиком под габариты помещений брифа; обмер и проект АР — задание (К-1); высота потолка 2900 мм — по брифу, не замерена; перекрытие 330 мм и отметка 2-го этажа +3,230 приняты; проект КР — задание (К-2); наружные стены 400 мм, перегородки 120 мм приняты (в брифе толщин нет) (К-1); разрешённая мощность 15 кВт принята по типовым ТУ для частного дома (К-4); подрайон климата не задан — принят не северный (жилые от 2,5 м) (К-7).

См. лист открытых вопросов (лист 7, записи К-1, К-2, К-4; лист 8, запись К-7).

Общие указания — лист 6: ±0,000 — чистый пол 1-го этажа; несущие конструкции и сети — по отдельному проекту; скрытые работы — по актам. Вопросы и допущения — листы 7–9.

Изм.	Кол.уч	Лист	№ док.	Подп.	Дата
Разраб.		Кырлан А.С.			04.11.26
Пров.					
ГИП					
Н. контр.					
Утв.					

ГД-2026-012-АИ

Дом 120 м²

Общая площадь 147,36* м² · * размеры приняты, не замерены (реестр — л. 7–9, К-1)

Дизайн-проект интерьера

Стадия	Лист	Листов
РП	5	175

Общие данные

М б/м

Кырлан Александр Сергеевич

выпуск 04.11.2026 № 4dfa962484 · стр. 5 из 180

Общие данные

Комплект ГД-2026-012-АИ · лист 5 общих данных (продолжение)

ПРЕДВАРИТЕЛЬНО · не для производства работ · открыто пунктов: 11 (реестр — л. 7–9)

Ведомость ссылочных и прилагаемых документов (продолжение)

Обозначение	Наименование	Примечание
ГД-2026-012-АИ.В16	Визуализация. Интерьер: Гостиная-кухня (пом. 1), стена Б	
ГД-2026-012-АИ.В17	Визуализация. Интерьер: Гостиная-кухня (пом. 1), стена В	
ГД-2026-012-АИ.В18	Визуализация. Интерьер: Кабинет (пом. 3), стена А	
ГД-2026-012-АИ.В19	Визуализация. Интерьер: Кабинет (пом. 3), стена В	
ГД-2026-012-АИ.В20	Визуализация. Интерьер: Гардеробная (пом. 8), общий вид	
ГД-2026-012-АИ.В21	Визуализация. Интерьер: Санузел гостевой (пом. 4), общий вид	

Состав дизайн-проекта

Раздел	Состав	Листы
Обложка	Дизайн-проект интерьера; Дом 120 м²; автор проекта — Кырлан Александр Сергеевич	1 с.
Концепция	Стиль Средиземноморский 60 % + Скандинавский 40 %: концепция интерьера, палитра и материалы (колерная карта — лист 83)	л. 25
Визуализации	21 изобр.: Вид сверху (3D): планировка с мебелью, текстилем и декором; Вид сверху (3D): планировка с мебелью, текстилем и декором; Санузел второго этажа, общий вид; Спальня родителей, стена В; Спальня родителей, стена Г; Холл с лестницей, стена Б; Холл второго этажа, общий вид; Коридор второго этажа, общий вид; Прихожая, стена А; Прихожая, стена Б; Детская, стена А; Детская, стена В; Детская вторая, стена А; Детская вторая, стена Г; Гостиная-кухня, стена А; Гостиная-кухня, стена Б; Гостиная-кухня, стена В; Кабинет, стена А; Кабинет, стена В; Гардеробная, общий вид; Санузел гостевой, общий вид	В1–В21
Рабочие чертежи	планы, развёртки, узлы (развёртки и узлы — листы 59–62, 116, 117, 134, 136, 142, 152–154, 158, 164, 167, 168)	л. 1–175
Спецификации и ведомости	оборудование, изделия, отделка, электроточки	л. 23, 29–33, 40, 41, 63, 80–87, 92–94, 120, 125, 141, 169–173

Условные обозначения

- контрольный отрезок 1000 мм натуры: по нему проверяют печать 1:1
- отметка уровня, м: ±0,000 — чистый пол 1-го этажа
- марка развёртки: буква стены, стрелка — взгляд
- О1 — марка отделки по реестру отделки альбома
- выноска узла: над полкой — узел, под полкой — лист

Допущения и предложения на листе

Основа листа: взаимное расположение помещений, контур дома 9600 × 8000 и раскладка этажей подобраны проектировщиком под габариты помещений брифа; обмер и проект АР — задание (К-1); высота потолка 2900 мм — по брифу, не замерена; перекрытие 330 мм и отметка 2-го этажа +3,230 приняты; проект КР — задание (К-2); наружные стены 400 мм, перегородки 120 мм приняты (в брифе толщин нет) (К-1); разрешённая мощность 15 кВт принята по типовым ТУ для частного дома (К-4); подрайон климата не задан — принят не северный (жилые от 2,5 м) (К-7).

См. лист открытых вопросов (лист 7, записи К-1, К-2, К-4; лист 8, запись К-7).

Общие указания

1. Рабочие чертежи интерьера разработаны на основании задания на проектирование и обмерного плана (лист 17). Объект: Дом 120 м²; автор проекта — Кырлан Александр Сергеевич; общая площадь 147,36 м², жилая 81,02 м², помещений 13.
2. Рабочие чертежи выполнены в соответствии с заданием на проектирование и нормативными документами, перечисленными в п. 4.
3. Открытые вопросы, принятые допущения и конфликты между разделами, не снятые к выпуску комплекта, сведены в таблицы на листах 7–9. До ответа по пункту таблицы показанное на указанном там листе — допущение, а не утверждённое решение: комплект по этим листам предварительный.
4. Нормативные документы, на которые есть ссылки в листах комплекта: ГОСТ Р 21.101-2026; ГОСТ 21.501-2018; ГОСТ 2.302-68; ГОСТ 2.303-68; ГОСТ 2.304-81; ГОСТ 2.307-2011; СП 54.13330.2022; СП 71.13330.2017; СП 73.13330.2016; ПУЭ (7-е изд.), гл. 1.8, 7.1; ГОСТ Р 50571.7.701-2024; СанПиН 1.2.3685-21; ГОСТ 2.702; ГОСТ 2.755; ГОСТ 21.110-2013; ГОСТ 21.601; ГОСТ 13996-2019; ГОСТ 23166-2021; ГОСТ 25772-2025; ГОСТ 31173-2016; ГОСТ 31565-2012; ГОСТ 32414-2013; ГОСТ 32415-2013; ГОСТ Р 56387-2018; ГОСТ Р 56926; СП 20.13330.2016; СП 29.13330.2011; СП 30.13330.2020; СП 55.13330.2016; СП 59.13330.2020; СП 131.13330. Документы из ведомости ссылочных документов здесь не повторяются.
5. За отметку ±0,000 принят уровень чистого пола 1-го этажа дома (условная нулевая отметка; абсолютная — по проекту дома); отметки чистого пола этажей: 2-й этаж +3,230 — отметки уровней этажа на листах даны от ±0,000 здания. Отметка чистого пола мокрых помещений — −0,015, +3,215. Размеры — в миллиметрах, отметки — в метрах, площади — в м²; высоты установки Н — от чистого пола своего помещения до оси изделия.
6. Несущие конструкции, общедомовые стояки, вентиляционные каналы и инженерные сети дома настоящим комплектом не изменяются. Работы, затрагивающие их (проём или штраба в несущей стене, перенос стояка, врезка в вентканал, расширение мокрой зоны), выполняются только по отдельному проекту, к которому прилагается техническое заключение о допустимости и безопасности работ, выданное автором проекта дома или организацией с допуском на обследование, и который согласован в установленном порядке (Жилищный кодекс РФ, ст. 25–29).
7. Трассы инженерных сетей на листах — принципиальные. Расчёты электрических нагрузок и токов КЗ, гидравлики, воздухообмена, освещённости и нагрузок на перекрытие выполняются в проектах ЭОМ, ВК, ОВ и КР организацией с допуском СРО; фактические трассы до закрытия отделкой фиксируются исполнительными схемами.
8. Стиль интерьера — Средиземноморский 60 % + Скандинавский 40 %. Палитра проекта: основной 60 % — Tikkurila G503 «Calla», Little Greene No. 222 «Loft White»; дополнительный 30 % — NCS S 1010-Y20R «Светлый песок / известняк», Farrow & Ball No. 89 «Lulworth Blue — светлая морская лазурь», Farrow & Ball No. 292 «Treron — серо-оливковая листва»; акцент 10 % — NCS S 3050-R80B «Эгейский синий», Farrow & Ball No. 66 «India Yellow — охра / горчица итальянских фасадов», NCS S 5020-G90Y «Олива». Коды цвета — по веерам производителей; цвет утверждается по выкрасу на объекте при освещении проекта.
9. Площади поверхностей — по чистым граням стен до отделки: стены = периметр × высоту от чистого пола помещения до низа потолка минус проёмы (облицовка плиткой — до верха облицовки); плинтус = периметр минус дверные проёмы; пол и потолок — по площади помещения. Количество плиток — по раскладке. Способ один для всех листов комплекта (ведомость отделки, колерная карта, раскладка плитки, развёртки).
10. Марки: стены помещения на всех листах — А (верхняя по плану), Б (правая), В (нижняя), Г (левая); марка отделки О — одна на весь альбом; реестр марок отделки (с позициями колерной карты той же отделки) и марки позиций по видам — на листе 114.
11. Развёртки стен выполнены по всем помещениям для стен с электроточками, мебелью, декором и отделкой: санузлы и кухонный фронт — в М 1:25, остальные стены — в М 1:25; расположение развёрток и узлов — на листе 116, узлы — на листе 168.
12. Перечень скрытых работ, на которые составляются акты освидетельствования (форма по приказу Минстроя России № 344/пр): гидроизоляция пола и стен мокрых помещений (с тестом проливом); стяжка пола (толщина, прочность, влажность основания); скрытая электропроводка (за потолком и в штробах стен; условия штробления — в следующем пункте); трубопроводы водоснабжения и канализации до закрытия (опрессовка, уклоны); закладные и усиления под подвесные приборы, мебель и тяжёлый декор, рамы инсталляций; короба дверей скрытого монтажа до штукатурки; каркасы ГКЛ потолков, коробов и перегородок до обшивки.
13. Скрытая электропроводка: за потолком и в штробах стен. Штробы в стенах выполняются только после технического заключения о несущих конструкциях; до заключения несущие стены не определены, и все стены считаются несущими; объём штроб — в ведомости объёмов работ, строка «Штробы в стенах» (вертикальные спуски; объём не меньше фактического, горизонтальные трассы — по исполнительной схеме).
14. Критерии приёмки: допуски отделочных покрытий — по СП 71.13330.2017; испытания систем водоснабжения и канализации — по СП 73.13330.2016 до закрытия трасс; приёмо-сдаточные испытания электроустановки — по ПУЭ, гл. 1.8, с протоколом электролаборатории.
15. Осознанные отступления от ГОСТ Р 21.101-2026, принятые в комплекте: номер листа и число листов («Листов») указаны на каждом листе; на масштабных листах в основной надписи указан фактический масштаб и дан контрольный отрезок 1000 мм; развёртки стен выполнены в М 1:25 (ГОСТ 21.507-81 — 1:50…1:500) ради читаемости привязок; размерные числа и марки элементов (Д-1, ОК-1, О6) кеглем 2,5 мм, номера помещений — в кружке Ø 8 мм (канон — 3,5 мм и Ø 12 мм): так насыщенные листы А3 читаются без наложений надписей.
16. Графы «Пров.», «Н. контр.», «Утв.» основной надписи заполняются при согласовании комплекта с заказчиком; до согласования комплект подписывает автор проекта (графа «Разраб.»).

Изм.	Кол.уч	Лист	№ док.	Подп.	Дата	ГД-2026-012-АИ		
						Дом 120 м²		
						Общая площадь 147,36* м² · * размеры приняты, не замерены (реестр — л. 7–9, К-1)		
Разраб.		Кырлан А.С.			04.11.26	Дизайн-проект интерьера	Стадия: РП	Лист: 6 / Листов: 175
Пров.								
ГИП								
Н. контр.								
Утв.						Общие данные · М б/м	Кырлан Александр Сергеевич	

выпуск 04.11.2026 № 4dfa962484 · стр. 6 из 180

Открытые вопросы, принятые допущения и конфликты. Лист 1 из 3

ПРЕДВАРИТЕЛЬНО · не для производства работ · открыто пунктов: 11 (реестр — л. 7–9)

Сводка по реестрам координации (стартовое совещание 19.10.2026)

Комплект предварительный по пунктам этих таблиц. Пока по пункту нет ответа или решения, показанное на указанном листе — допущение проектировщика, а не утверждённое решение.
Сводка: открытых вопросов — 9 (из них ждут факта объекта — 3: контрольного обмера, обследования или документа); изменений в реестре — 2, из них без подписи — 2.
Пункты, ответ на которые лежит на объекте, а не за столом проектировщика (графа «Вид», строка «Ждёт»), собраны на листе «Задание на контрольный обмер и обследование» (листы 10–13): что и где замерить, с какой точностью и чем подтвердить. Пункты, ждущие решения человека, на объекте не закрываются.

Открытые вопросы и принятые допущения

№	Формулировка	Вид	Кто решает	Если решения нет	Лист, где это проявляется
К-1	Бриф задаёт 11 помещений с габаритами и этажами, но не их взаимное расположение, контур дома и толщины стен: раскладка этажей, контур 9600 × 8000 и перегородки подобраны проектировщиком под габариты брифа. До заказа мебели, дверей и материалов нужен обмер или проект дома (АР).	Отсутствует Ждёт: обмера	Архитектор-планировщик	размеры на листах — предложение проектировщика по брифу, уточняются по месту; мебель на заказ и материалы по ним не заказывать	л. 17, 18 — Обмерный план л. 17–22, 25–28, 34–39, 44–55, 61, 62, 66, 67, 77–79, 83, 84, 89, 90, 96, 97, 116, 117, 155–159, 164–167 — 1-й этаж л. 27, 28 — План расстановки мебели л. 17–22, 25–28, 34–39, 44–55, 61, 62, 66, 67, 77–79, 83, 84, 89, 90, 96, 97, 116, 117, 155–159, 164–167 — 1-й этаж
К-2	Высота потолка 2900 мм — по брифу (не замерена); конструкция и толщина перекрытия не заданы — принято 330 мм с полом, отметка чистого пола 2-го этажа +3,230. Нужен проект КР дома.	Отсутствует	Архитектор-планировщик	высоты на развёртках, отметка 2-го этажа и лестница — от принятых 2900 / +3,230, уточнить по проекту КР	л. 17, 18 — Обмерный план л. 17–22, 25–28, 34–39, 44–55, 61, 62, 66, 67, 77–79, 83, 84, 89, 90, 96, 97, 116, 117, 155–159, 164–167 — 1-й этаж л. 66, 67 — План потолков л. 17–22, 25–28, 34–39, 44–55, 61, 62, 66, 67, 77–79, 83, 84, 89, 90, 96, 97, 116, 117, 155–159, 164–167 — 1-й этаж
К-3	Лестница по брифу — из холла 1-го этажа; место, тип (одномаршевая прямая, 17 подъёмов 190 × 250, марш 1000), конструкция и ограждение — предложение проектировщика. Расчёт несущей конструкции марша и проёма в перекрытии — проект КР.	Отсутствует	Архитектор-планировщик	лестница на планах — предложение, к изготовлению не выдаётся до проекта КР	л. 17, 18 — Обмерный план л. 17–22, 25–28, 34–39, 44–55, 61, 62, 66, 67, 77–79, 83, 84, 89, 90, 96, 97, 116, 117, 155–159, 164–167 — 1-й этаж
К-4	Разрешённая мощность дома по ТУ неизвестна, принята 15 кВт.	Отсутствует	Инженер-электрик	щит и группы рассчитаны на 15 кВт; при других ТУ пересчёт	л. 42 — Однолинейная схема щита л. 34, 35 — План розеток и электровыводов л. 17–22, 25–28, 34–39, 44–55, 61, 62, 66, 67, 77–79, 83, 84, 89, 90, 96, 97, 116, 117, 155–159, 164–167 — 1-й этаж
К-5	Тип дома, материал и конструкция стен и перекрытия, несущие стены, положение стояков, выпусков канализации и вентканалов в брифе не заданы; проект дома (АР, КР, ВК, ОВ) не передан. Стояки и вентканалы на планах показаны по предложению проектировщика.	Отсутствует Ждёт: документа	Архитектор-планировщик	все существующие стены считаются несущими: проёмы и перегородки — предложение, к строительству не выдаются; стояки — предложение	л. 17, 18 — Обмерный план л. 17–22, 25–28, 34–39, 44–55, 61, 62, 66, 67, 77–79, 83, 84, 89, 90, 96, 97, 116, 117, 155–159, 164–167 — 1-й этаж л. 54, 55 — Схема разводки водопровода и канализации л. 17–22, 25–28, 34–39, 44–55, 61, 62, 66, 67, 77–79, 83, 84, 89, 90, 96, 97, 116, 117, 155–159, 164–167 — 1-й этаж
К-6	Источник отопления и горячей воды (котёл: газ / электро, его место, котельная) брифом не задан; в составе помещений брифа котельной нет. Отопительные приборы на листах — водяные радиаторы под окнами при любом источнике тепла.	Решение	Инженер ОВ	радиаторы и трассы — предложение; котёл, котельная и ввод газа — после ответа заказчика	л. 50, 51 — План отопления л. 17–22, 25–28, 34–39, 44–55, 61, 62, 66, 67, 77–79, 83, 84, 89, 90, 96, 97, 116, 117, 155–159, 164–167 — 1-й этаж л. 54, 55 — Схема разводки водопровода и канализации л. 17–22, 25–28, 34–39, 44–55, 61, 62, 66, 67, 77–79, 83, 84, 89, 90, 96, 97, 116, 117, 155–159, 164–167 — 1-й этаж

						ГД-2026-012-АИ	
						Дом 120 м²	
						Общая площадь 147,36* м² · * размеры приняты, не замерены (реестр — л. 7–9, К-1)	
Изм.	Кол.уч	Лист	№ док.	Подп.	Дата	Дизайн-проект интерьера	Стадия: РП; Лист: 7; Листов: 175
Разраб.		Кырлан А.С.			04.11.26		
Пров.							
ГИП							
						Открытые вопросы, принятые допущения и конфликты. Лист 1 из 3 М б/м	**Кырлан Александр Сергеевич**
Н. контр.							
Утв.							

выпуск 04.11.2026 № 4dfa962484 · стр. 7 из 180

Открытые вопросы, принятые допущения и конфликты. Лист 2 из 3

Сводка по реестрам координации (стартовое совещание 19.10.2026)

Открытые вопросы и принятые допущения (продолжение)

№	Формулировка	Вид	Кто решает	Если решения нет	Лист, где это проявляется
К-7	Климатический подрайон (СП 131.13330) не задан: принят не северный — жилые комнаты и кухня под потолком от 2,5 м (СП 54, п. 5.12); в IA, IБ, IГ, IД, IVA — от 2,7 м.	Отсутствует Ждёт: документа	Архитектор-планировщик	отметки потолков жилых — по 2,5 м; при северном подрайоне уровни ниже 2,7 м пересчитать до заказа каркаса	л. 66, 67 — План потолков л. 17–22, 25–28, 34–39, 44–55, 61, 62, 66, 67, 77–79, 83, 84, 89, 90, 96, 97, 116, 117, 155–159, 164–167 — 1-й этаж
К-8	Кухня (пом. 1): мойка Кх2 и модули Кх1, Кх3 стоят под окном 1500 × 1500 стены А с низом проёма +0,900 — подоконник в уровне столешницы (+0,900). Смеситель мойки упирается в створку, открывающуюся внутрь, примыкание столешницы к откосу и подоконнику не решено. Нужно решение заказчика: створка над мойкой глухая или поворотно-откидная (откидывание над смесителем), либо поднять низ окна (подоконник выше столешницы на высоту смесителя), либо столешница заходит в проём вместо подоконника.	Решение Ждёт: решения	Дизайнер интерьера	столешница у окна не раскраивается, мойка Кх2 и смеситель не заказываются; монтажная схема кухни показывает проём и конфликт	л. 108 — Кухня (пом. 1). Монтажная схема
К-9	Умывальник См4 (пом. 13 «Санузел второго этажа»), выпуск К1-4 Ø50: трасса до Ст К1-1 (2,54 м) идёт под дверным проёмом Д-8 — короб над полом там не поставить. Решить: (а) прибор ближе к стояку Ст К1-1 (без прохода под проёмом); (б) выпуск в полу с подъёмом пола помещения на 130 мм; (в) насосная установка (КНС) у прибора — по паспорту, требует согласования. Решение меняет санузел (высоты, раскладку плитки) — за автором с заказчиком.	Спорно Ждёт: решения	Инженер ВК (вода, канализация)	выпуск К1-4 и прибор См4 не выполнять до решения; остальное — по листам	л. 54, 55 — Схема разводки водопровода и канализации л. 17–22, 25–28, 34–39, 44–55, 61, 62, 66, 67, 77–79, 83, 84, 89, 90, 96, 97, 116, 117, 155–159, 164–167 — 1-й этаж л. 52, 53 — План выводов сантехники л. 17–22, 25–28, 34–39, 44–55, 61, 62, 66, 67, 77–79, 83, 84, 89, 90, 96, 97, 116, 117, 155–159, 164–167 — 1-й этаж

Изм.	Кол.уч	Лист	№ док.	Подп.	Дата	ГД-2026-012-АИ		
						Дом 120 м²		
						Общая площадь 147,36* м² · * размеры приняты, не замерены (реестр — л. 7–9, К-1)		
Разраб.		Кырлан А.С.			04.11.26	Дизайн-проект интерьера	Стадия: РП	Лист: 8 / Листов: 175
Пров.								
ГИП								
						Открытые вопросы, принятые допущения и конфликты. Лист 2 из 3 М б/м	**Кырлан Александр Сергеевич**	
Н. контр.								
Утв.								

выпуск 04.11.2026 № 4dfa962484 · стр. 8 из 180

Открытые вопросы, принятые допущения и конфликты. Лист 3 из 3

Сводка по реестрам координации (стартовое совещание 19.10.2026)

Изменения проекта после выпуска листов (реестр изменений)

№	Дата	Лист	Было	Стало	Кто решил, подпись
ИЗ-1	30.10.2026	л. 52, 53 — План выводов сантехники л. 17–22, 25–28, 34–39, 44–55, 61, 62, 66, 67, 77–79, 83, 84, 89, 90, 96, 97, 116, 117, 155–159, 164–167 — 1-й этаж л. 54, 55 — Схема разводки водопровода и канализации л. 17–22, 25–28, 34–39, 44–55, 61, 62, 66, 67, 77–79, 83, 84, 89, 90, 96, 97, 116, 117, 155–159, 164–167 — 1-й этаж л. 27, 28 — План расстановки мебели л. 17–22, 25–28, 34–39, 44–55, 61, 62, 66, 67, 77–79, 83, 84, 89, 90, 96, 97, 116, 117, 155–159, 164–167 — 1-й этаж л. 21, 22 — План дверей л. 17–22, 25–28, 34–39, 44–55, 61, 62, 66, 67, 77–79, 83, 84, 89, 90, 96, 97, 116, 117, 155–159, 164–167 — 1-й этаж л. 34, 35 — План розеток и электровыводов л. 17–22, 25–28, 34–39, 44–55, 61, 62, 66, 67, 77–79, 83, 84, 89, 90, 96, 97, 116, 117, 155–159, 164–167 — 1-й этаж л. 77 — Раскладка плитки. Санузел второго этажа. Развёртки стен	Санузел второго этажа (пом. 13, 2600×2200): раковина См4 (стена А 500…1100) и стиральная машина См3 (стена Г 300…900) пересекались в углу, перед люком машины стояла раковина; ванна См1 (стена В 150…1850) заходила в проход перед Д-8 на 500 из 800 мм; унитаз См2 (стена Б 900…1300) накрывал стояки Ст К1-1 / В1-1; полотенцесушитель См5 в 2,3 м от стояка ГВС; при открытом полотне Д-8 в помещение не пройти.	Ванна См1 — вдоль стены Г (offset 500, х 3800…4550, у 6300…8000); умывальник См4 — стена А offset 800…1400; стиральная машина См3 — стена В offset 1200…1800 (перед люком 1150 мм); унитаз См2 — стена Б offset 1150…1550 (250 мм до стояков — короб с люком); полотенцесушитель См5 — стена Б 1600…2100; Д-8 — петли у правого откоса. Точки ЭОМ санузла перенесены за приборами (Р7 — стена В, Р8 — offset 1500, Св15 — 1100, КУП1 и В6 — стена Б). Трасса выпуска умывальника под проёмом Д-8 остаётся — К-9. Знак «**» у приборов до подписи автора.	Не утверждено: подписи нет. решение исполнителя; предложение проектировщика, на утверждение А. С. Кырлана
ИЗ-2	30.10.2026	л. 27, 28 — План расстановки мебели л. 17–22, 25–28, 34–39, 44–55, 61, 62, 66, 67, 77–79, 83, 84, 89, 90, 96, 97, 116, 117, 155–159, 164–167 — 1-й этаж л. 127 — Развёртка стены А. Холл с лестницей (пом. 2) л. 132 — Развёртка стены В. Кабинет (пом. 3) л. 150 — Развёртка стены В. Детская (пом. 7) л. 155 — Развёртка стены А. Холл второго этажа (пом. 10) л. 162 — Развёртка стены В. Детская вторая (пом. 12) л. 34, 35 — План розеток и электровыводов л. 17–22, 25–28, 34–39, 44–55, 61, 62, 66, 67, 77–79, 83, 84, 89, 90, 96, 97, 116, 117, 155–159, 164–167 — 1-й этаж	Мебель закрывала радиаторы: банкетка Хл1 (холл) на Рд3, стол Кб1 (кабинет) на Рд4, стол Дт2 (детская) на Рд6, стеллаж Хл2 (холл 2-го этажа) перед Рд7, стол Дт7 (детская вторая) на Рд8; на пяти развёртках — служебная фраза «прибор в корпусе не решён». Розетка Р16 прихожей за радиатором Рд2. Назначения Р9/Р10 «у кровати» и Р11 «у комода» в кабинете, Р42/Р47 «у комода» в детских — по образцу, не по мебели. Группы щита 15–17 без точек на планах.	Хл1 и Хл2 — у стены Г холлов (offset 1200); столы Кб1, Дт2, Дт7 — 300 мм от лицевой плоскости радиатора (х,у), стулья за ними; радиаторы открыты. Р16 — стена В offset 2300; Р34 — offset 2600. Назначения точек переписаны по расстановке. Р7 (стиральная машина) — группа 15, Р8, Р33, В6 (фены, полотенцесушитель) — группа 16, Р17 (ЩС) — группа 17. Знак «**» у переставленной мебели до подписи автора.	Не утверждено: подписи нет. решение исполнителя; предложение проектировщика, на утверждение А. С. Кырлана

Примечания

1. Номера листов — по ведомости рабочих чертежей комплекта (лист «Общие данные»).
2. Графа «Если решения нет» показывает состояние решения на листах; влияние на сроки и стоимость по пунктам не оценивалось.
3. Пункт, по которому принято решение, при следующем выпуске комплекта из таблиц исключается.

Изм.	Кол.уч	Лист	№ док.	Подп.	Дата
Разраб.		Кырлан А.С.			04.11.26
Пров.					
ГИП					
Н. контр.					
Утв.					

ГД-2026-012-АИ

Дом 120 м²

Общая площадь 147,36* м² · * размеры приняты, не замерены (реестр — л. 7–9, К-1)

Дизайн-проект интерьера

Стадия	Лист	Листов
РП	9	175

Открытые вопросы, принятые допущения и конфликты. Лист 3 из 3

М б/м

Кырлан Александр Сергеевич

Задание на контрольный обмер и обследование. Лист 1 из 4

Что замерить, вскрыть и получить до заказа материалов и изделий

Задание собрано из открытых вопросов, ответ на которые лежит на объекте или в документах, а не за столом проектировщика. Пока факт не получен, размер, материал или положение на листах — допущение (знак «*»), а не замер.
Сводка: на объекте — 21 (до демонтажа — 19; после демонтажа — 2); документом и при закупке — 3; из допущений в данных и на листах — 22, из них без вопроса в реестре — 4. Закрываются вопросы: К-1, К-2, К-4, К-5, К-7 (5). Вопросы, ждущие решения человека, задание не закрывает — они решаются по реестру открытых вопросов.

Условия проведения

Порядок работ	Приёмы и точность	Кто присутствует	Если факт не совпал с проектом
1. До демонтажа — существующее состояние: контур, диагонали, высоты, проёмы, оси стояков, ниши и конструкции, которые видны. 2. После демонтажа, до черновых работ — то, что закрывали отделка и короба: основание стен, фактические толщины, углы, узлы. 3. Документы и данные закупки — не на объекте: к сроку из последней таблицы, от них зависят привязки и заказ. Что заказывается по размеру из задания, до закрытия пункта не заказывают: сроки изготовления — по графику закупок прораба.	Обход по часовой стрелке от входа: стены, проёмы, потолок, коммуникации (стояки, щиток, вентканалы), особенности (ниши, короба, выступы). Размеры записывают в мм; сумма участков равна общему размеру, при цепочке длиннее трёх участков ставят проверочный (общий) размер. Диагонали каждого помещения; если две диагонали различаются на 5 мм и больше, разницу подписывают на плане. Потолок — в нескольких точках: центр, углы, у проёмов. Проём — ширина, высота, глубина откоса, привязка к ближайшим углам, высота подоконника. Допустимая погрешность прибора — 2–3 мм на метр; размеры округляют кратно 5 мм; два контрольных промера одного размера не должны расходиться более чем на 2 %. Допуск по пункту — в графе «Точность». План БТИ обмер не заменяет.	Прораб (отвечает за проведение) — назначает день и порядок обхода, открывает объект и освобождает помещения, ведёт это задание и реестр изменений. Архитектор — выполняет обмер, составляет акт контрольного обмера и подписывает результаты по размерам и конструкциям. Владельцы вопросов присутствуют при пунктах своего раздела или принимают результат до заказа: Инженер-электрик — К-4; позиции О-1; Инженер ОВ — позиции О-2; Отделочник — позиции О-20, О-21. Заказчик или его представитель — передаёт документы (план БТИ, проект дома, технические условия, паспорта), подписывает акт. Проектных решений на обмере не принимают: обмер даёт факт, решения — по реестру открытых вопросов (листы 7–9).	1. В пределах допуска пункта — принимается измеренное значение, лист перевыпускается, знак «*» снимается. 2. Больше допуска или контрольные промеры расходятся более чем на 2 % — промер повторяют; не подтвердилось — запись в реестр изменений (дата, лист, было, стало, кто решил, подпись), работы в этом месте не начинают. 3. Затронуты несущая стена, стояк, вентканал или мокрая зона — сразу владельцу раздела и ГИПу (главному инженеру проекта); между разделами не больше двух кругов, затем решает ГИП. 4. На объекте устно ничего не согласуется: каждое решение — записью в реестр с подписью.

Этап 1. До демонтажа

№	Где	Способ	Что сделать	Кто выполняет	Точность	Что пересчитается в альбоме	Чем подтверждается	Закрывает вопросы реестра
О-1	Вход в квартиру или лестничная клетка; место щита на плане	Обмер	Существующий щиток и счётчик электроэнергии: место и габарит ниши, состояние ввода, марка и сечение вводного кабеля, наличие вводного автомата и УЗО, пломбы.	Архитектор	±5 мм	Ниша и место щита на листах; вводной кабель и аппараты на однолинейной схеме; расстояния до первых групп. Листы: л. 42, 43 — Однолинейная схема щита	акт контрольного обмера; фото с рулеткой и привязкой к стене или углу	Вопроса в реестре нет: Альбом принимает щит и ввод без осмотра. Результат принимает: Инженер-электрик
О-2	у окон	Обмер	Положение стояков отопления (подающий и обратный) от граней стен, диаметры, наличие запорной арматуры; существующие радиаторы: число секций, межосевое расстояние, подводки. В данных стояков отопления нет — лист отопления выводит их условно у откоса окна.	Архитектор	±5 мм	План отопления: места стояков и подводок, привязки радиаторов; подбор радиаторов по теплотехническому расчёту; радиаторы и узлы подключения в ВОР и спецификации. Листы: л. 50, 51 — План отопления	акт контрольного обмера; фото с рулеткой и привязкой к стене или углу	Вопроса в реестре нет: Альбом принимает положение стояков и радиаторов отопления без обмера. Результат принимает: Инженер ОВ
О-3	все помещения	Обмер	Обмер всех помещений обоих этажей: стороны, диагонали, проёмы, высота потолка, проём лестницы.	исполнитель	±5 мм; диагонали — разница от 5 мм подписывается	обмерный и монтажный планы, развёртки, мебель на заказ Листы: л. 17, 18 — Обмерный план л. 17–22, 25–28, 34–39, 44–55, 61, 62, 66, 67, 77–79, 83, 84, 89, 90, 96, 97, 116, 117, 155–159, 164–167 — 1-й этаж л. 27, 28 — План расстановки мебели	акт контрольного обмера	К-1 Результат принимает: Архитектор
О-4	Все помещения квартиры	Обмер	Высота потолка в каждом помещении в нескольких точках: центр, углы, у проёмов.	Архитектор	±5 мм	Вертикальные размеры альбома: развёртки, шкафы, плитка, объёмы работ. Листы: л. 2–6 — Общие данные	акт контрольного обмера	К-2 Результат принимает: Архитектор

Допущения и предложения на листе
Основа листа: взаимное расположение помещений, контур дома 9600 × 8000 и раскладка этажей подобраны проектировщиком под габариты помещений брифа; обмер и проект АР — задание (К-1); высота потолка 2900 мм — по брифу, не замерена; перекрытие 330 мм и отметка 2-го этажа +3,230 приняты; проект КР — задание (К-2); наружные стены 400 мм, перегородки 120 мм приняты (в брифе толщин нет) (К-1); разрешённая мощность 15 кВт принята по типовым ТУ для частного дома (К-4); подрайон климата не задан — принят не северный (жилые от 2,5 м) (К-7).
См. лист открытых вопросов (лист 7, записи К-1, К-2, К-4; лист 8, запись К-7).

Изм.	Кол.уч	Лист	№ док.	Подп.	Дата
Разраб.		Кырлан А.С.			04.11.26
Пров.					
ГИП					
Н. контр.					
Утв.					

ГД-2026-012-АИ

Дом 120 м²

Общая площадь 147,36* м² · * размеры приняты, не замерены (реестр — л. 7–9, К-1)

Дизайн-проект интерьера	Стадия	Лист	Листов
	РП	10	175

Задание на контрольный обмер и обследование.
Лист 1 из 4
М б/м

Кырлан Александр Сергеевич

Задание на контрольный обмер и обследование. Лист 2 из 4

Что замерить, вскрыть и получить до заказа материалов и изделий

ПРЕДВАРИТЕЛЬНО · не для производства работ · открыто пунктов: 11 (реестр — л. 7–9)

Этап 1. До демонтажа (продолжение)

№	Где	Способ	Что сделать	Кто выполняет	Точность	Что пересчитается в альбоме	Чем подтверждается	Закрывает вопросы реестра
О-5	Санузел гостевой (пом. 4): Ст К1-1*, Ст В1-1, Ст Т3-1*; Гостиная-кухня (пом. 1): Ст К1-2 (кухня)*, Ст В1-2*, Ст Т3-2*; наличие стояка ГВС, арматуры и счётчиков — по всей квартире	Обмер	Положение стояков Ст К1-1*, Ст В1-1*, Ст Т3-1*, Ст К1-2 (кухня)*, Ст В1-2, Ст Т3-2*: привязка осей от граней стен, диаметры, размеры короба и люков. Стояк горячей воды Т3 в данных не задан, на листах ВК принят рядом с стояком холодной воды: выяснить, есть ли он в доме, и где. Отключающая арматура и счётчики воды на вводах: положение, тип, пломбы управляющей компании. Сверить до разметки выводов.	Архитектор	±5 мм	Привязки выводов воды и канализации на планах выводов и разводки; расстояние розеток до стояка; места люков 300 × 400 мм; трассы Т3 и полотенцесушители (водяной или электрический); узлы ввода в спецификации ВК (краны, фильтры, счётчики). Листы: л. 52, 53 — План выводов сантехники л. 54, 55 — Схема разводки водопровода и канализации л. 63 — Спецификация сантехнического оборудования	акт контрольного обмера; фото с рулеткой и привязкой к стене или углу	К-5 Результат принимает: Архитектор
О-6	По месту	Обмер	Подтвердить на объекте принятое: подрайон климата не задан — принят не северный (жилые от 2,5 м)	Архитектор	±5 мм	Листы, где используется принятая величина. Листы: л. 2–6 — Общие данные	акт контрольного обмера	К-7 Результат принимает: Архитектор
О-7	Гостиная-кухня (пом. 1): окно пом. 1, стена А, окно пом. 1, стена А, дверь пом. 1, стена Б	Обмер	Окно пом. 1, стена А, окно пом. 1, стена А, дверь пом. 1, стена Б: положение (привязки к ближайшим углам), ширина, высота, высота подоконника, глубина откоса. Принято в проекте: окно: место, ширина, высота и подоконник приняты по брифу, стена — по раскладке проектировщика (К-1), не замерены, проём: место и ширина приняты проектировщиком по брифу (раскладка этажей — К-1), не замерены.	Архитектор	±5 мм	Проёмы на обмерном плане и в ведомости проёмов; откосы и оконные работы в ВОР; привязки мебели и выводов к проёмам. Листы: л. 17, 18 — Обмерный план л. 23 — Ведомость заполнения проёмов	акт контрольного обмера; фото с рулеткой и привязкой к стене или углу	К-1 Результат принимает: Архитектор
О-8	Холл с лестницей (пом. 2): окно пом. 2, стена А	Обмер	Окно пом. 2, стена А: положение (привязки к ближайшим углам), ширина, высота, высота подоконника, глубина откоса. Принято в проекте: окно: место, ширина, высота и подоконник приняты по брифу, стена — по раскладке проектировщика (К-1), не замерены.	Архитектор	±5 мм	Проёмы на обмерном плане и в ведомости проёмов; откосы и оконные работы в ВОР; привязки мебели и выводов к проёмам. Листы: л. 17, 18 — Обмерный план л. 23 — Ведомость заполнения проёмов	акт контрольного обмера; фото с рулеткой и привязкой к стене или углу	К-1 Результат принимает: Архитектор
О-9	Кабинет (пом. 3): окно пом. 3, стена В, дверь пом. 3, стена Б	Обмер	Окно пом. 3, стена В, дверь пом. 3, стена Б: положение (привязки к ближайшим углам), ширина, высота, высота подоконника, глубина откоса. Принято в проекте: окно: место, ширина, высота и подоконник приняты по брифу, стена — по раскладке проектировщика (К-1), не замерены, проём: место и ширина приняты проектировщиком по брифу (раскладка этажей — К-1), не замерены.	Архитектор	±5 мм	Проёмы на обмерном плане и в ведомости проёмов; откосы и оконные работы в ВОР; привязки мебели и выводов к проёмам. Листы: л. 17, 18 — Обмерный план л. 23 — Ведомость заполнения проёмов	акт контрольного обмера; фото с рулеткой и привязкой к стене или углу	К-1 Результат принимает: Архитектор
О-10	Санузел гостевой (пом. 4): дверь пом. 4, стена В	Обмер	Дверь пом. 4, стена В: положение (привязки к ближайшим углам), ширина, высота, толщина стены в проёме. Принято в проекте: проём: место и ширина приняты проектировщиком по брифу (раскладка этажей — К-1), не замерены.	Архитектор	±5 мм	Проёмы на обмерном плане и в ведомости проёмов; привязки мебели и выводов к проёмам. Листы: л. 17, 18 — Обмерный план л. 23 — Ведомость заполнения проёмов	акт контрольного обмера; фото с рулеткой и привязкой к стене или углу	К-1 Результат принимает: Архитектор
О-11	Прихожая (пом. 5): дверь пом. 5, стена В, дверь пом. 5, стена А	Обмер	Дверь пом. 5, стена В, дверь пом. 5, стена А: положение (привязки к ближайшим углам), ширина, высота, толщина стены в проёме. Принято в проекте: входная дверь: место и ширина проёма приняты проектировщиком по брифу (без плана дома), не замерены, проём: место и ширина приняты проектировщиком по брифу (раскладка этажей — К-1), не замерены.	Архитектор	±5 мм	Проёмы на обмерном плане и в ведомости проёмов; привязки мебели и выводов к проёмам. Листы: л. 17, 18 — Обмерный план л. 23 — Ведомость заполнения проёмов	акт контрольного обмера; фото с рулеткой и привязкой к стене или углу	К-1 Результат принимает: Архитектор

Допущения и предложения на листе

Основа листа: взаимное расположение помещений, контур дома 9600 × 8000 и раскладка этажей подобраны проектировщиком под габариты помещений брифа; обмер и проект АР — задание (К-1); высота потолка 2900 мм — по брифу, не замерена; перекрытие 330 мм и отметка 2-го этажа +3,230 приняты; проект КР — задание (К-2); наружные стены 400 мм, перегородки 120 мм приняты (в брифе толщин нет) (К-1); разрешённая мощность 15 кВт принята по типовым ТУ для частного дома (К-4); подрайон климата не задан — принят не северный (жилые от 2,5 м) (К-7).

Знак «*» — принято, не замерено и не подтверждено (замерить на объекте): К-5: Ст К1-1, Ст В1-1, Ст Т3-1, Ст К1-2 (кухня), Ст В1-2, Ст Т3-2 — положение стояка принято проектировщиком (проект ВК дома не передан), не замерено.

См. лист открытых вопросов (лист 7, записи К-1, К-2, К-4, К-5; лист 8, запись К-7).

Изм.	Кол.уч	Лист	№ док.	Подп.	Дата
Разраб.		Кырлан А.С.			04.11.26
Пров.					
ГИП					
Н. контр.					
Утв.					

ГД-2026-012-АИ

Дом 120 м²

Общая площадь 147,36* м² · * размеры приняты, не замерены (реестр — л. 7–9, К-1)

Дизайн-проект интерьера

Стадия	Лист	Листов
РП	11	175

Задание на контрольный обмер и обследование.
Лист 2 из 4
М б/м

Кырлан Александр Сергеевич

выпуск 04.11.2026 № 4dfa962484 · стр. 11 из 180

Задание на контрольный обмер и обследование. Лист 3 из 4

ПРЕДВАРИТЕЛЬНО · не для производства работ · открыто пунктов: 11 (реестр — л. 7–9)

Что замерить, вскрыть и получить до заказа материалов и изделий

Этап 1. До демонтажа (продолжение)

№	Где	Способ	Что сделать	Кто выполняет	Точность	Что пересчитается в альбоме	Чем подтверждается	Закрывает вопросы реестра
О-12	Спальня родителей (пом. 6): окно пом. 6, стена А, дверь пом. 6, стена Б	Обмер	Окно пом. 6, стена А, дверь пом. 6, стена Б: положение (привязки к ближайшим углам), ширина, высота, высота подоконника, глубина откоса. Принято в проекте: окно: место, ширина, высота и подоконник приняты по брифу, стена — по раскладке проектировщика (К-1), не замерены, проём: место и ширина приняты проектировщиком по брифу (раскладка этажей — К-1), не замерены.	Архитектор	±5 мм	Проёмы на обмерном плане и в ведомости проёмов; откосы и оконные работы в ВОР; привязки мебели и выводов к проёмам. Листы: л. 17, 18 — Обмерный план л. 23 — Ведомость заполнения проёмов	акт контрольного обмера; фото с рулеткой и привязкой к стене или углу	К-1 Результат принимает: Архитектор
О-13	Детская (пом. 7): окно пом. 7, стена В, дверь пом. 7, стена Б	Обмер	Окно пом. 7, стена В, дверь пом. 7, стена Б: положение (привязки к ближайшим углам), ширина, высота, высота подоконника, глубина откоса. Принято в проекте: окно: место, ширина, высота и подоконник приняты по брифу, стена — по раскладке проектировщика (К-1), не замерены, проём: место и ширина приняты проектировщиком по брифу (раскладка этажей — К-1), не замерены.	Архитектор	±5 мм	Проёмы на обмерном плане и в ведомости проёмов; откосы и оконные работы в ВОР; привязки мебели и выводов к проёмам. Листы: л. 17, 18 — Обмерный план л. 23 — Ведомость заполнения проёмов	акт контрольного обмера; фото с рулеткой и привязкой к стене или углу	К-1 Результат принимает: Архитектор
О-14	Гардеробная (пом. 8): дверь пом. 8, стена Б	Обмер	Дверь пом. 8, стена Б: положение (привязки к ближайшим углам), ширина, высота, толщина стены в проёме. Принято в проекте: проём: место и ширина приняты проектировщиком по брифу (раскладка этажей — К-1), не замерены.	Архитектор	±5 мм	Проёмы на обмерном плане и в ведомости проёмов; привязки мебели и выводов к проёмам. Листы: л. 17, 18 — Обмерный план л. 23 — Ведомость заполнения проёмов	акт контрольного обмера; фото с рулеткой и привязкой к стене или углу	К-1 Результат принимает: Архитектор
О-15	Кладовая (пом. 9): дверь пом. 9, стена Б	Обмер	Дверь пом. 9, стена Б: положение (привязки к ближайшим углам), ширина, высота, толщина стены в проёме. Принято в проекте: проём: место и ширина приняты проектировщиком по брифу (раскладка этажей — К-1), не замерены.	Архитектор	±5 мм	Проёмы на обмерном плане и в ведомости проёмов; привязки мебели и выводов к проёмам. Листы: л. 17, 18 — Обмерный план л. 23 — Ведомость заполнения проёмов	акт контрольного обмера; фото с рулеткой и привязкой к стене или углу	К-1 Результат принимает: Архитектор
О-16	Холл второго этажа (пом. 10): окно пом. 10, стена А	Обмер	Окно пом. 10, стена А: положение (привязки к ближайшим углам), ширина, высота, высота подоконника, глубина откоса. Принято в проекте: окно: место, ширина, высота и подоконник приняты по брифу, стена — по раскладке проектировщика (К-1), не замерены.	Архитектор	±5 мм	Проёмы на обмерном плане и в ведомости проёмов; откосы и оконные работы в ВОР; привязки мебели и выводов к проёмам. Листы: л. 17, 18 — Обмерный план л. 23 — Ведомость заполнения проёмов	акт контрольного обмера; фото с рулеткой и привязкой к стене или углу	К-1 Результат принимает: Архитектор
О-17	Коридор второго этажа (пом. 11): дверь пом. 11, стена Б	Обмер	Дверь пом. 11, стена Б: положение (привязки к ближайшим углам), ширина, высота, толщина стены в проёме. Принято в проекте: проём: место и ширина приняты проектировщиком по брифу (раскладка этажей — К-1), не замерены.	Архитектор	±5 мм	Проёмы на обмерном плане и в ведомости проёмов; привязки мебели и выводов к проёмам. Листы: л. 17, 18 — Обмерный план л. 23 — Ведомость заполнения проёмов	акт контрольного обмера; фото с рулеткой и привязкой к стене или углу	К-1 Результат принимает: Архитектор
О-18	Детская вторая (пом. 12): окно пом. 12, стена В, дверь пом. 12, стена А	Обмер	Окно пом. 12, стена В, дверь пом. 12, стена А: положение (привязки к ближайшим углам), ширина, высота, высота подоконника, глубина откоса. Принято в проекте: окно: место, ширина, высота и подоконник приняты по брифу, стена — по раскладке проектировщика (К-1), не замерены, проём: место и ширина приняты проектировщиком по брифу (раскладка этажей — К-1), не замерены.	Архитектор	±5 мм	Проёмы на обмерном плане и в ведомости проёмов; откосы и оконные работы в ВОР; привязки мебели и выводов к проёмам. Листы: л. 17, 18 — Обмерный план л. 23 — Ведомость заполнения проёмов	акт контрольного обмера; фото с рулеткой и привязкой к стене или углу	К-1 Результат принимает: Архитектор
О-19	Санузел второго этажа (пом. 13): дверь пом. 13, стена А	Обмер	Дверь пом. 13, стена А: положение (привязки к ближайшим углам), ширина, высота, толщина стены в проёме. Принято в проекте: Петли у правого откоса (х 6150, у стояков): открытое полотно стоит вдоль стены Б, вошедший идёт влево к умывальнику и ванне. ИЗ-1..	Архитектор	±5 мм	Проёмы на обмерном плане и в ведомости проёмов; привязки мебели и выводов к проёмам. Листы: л. 17, 18 — Обмерный план л. 23 — Ведомость заполнения проёмов	акт контрольного обмера; фото с рулеткой и привязкой к стене или углу	К-1 Результат принимает: Архитектор

Допущения и предложения на листе

Основа листа: взаимное расположение помещений, контур дома 9600 × 8000 и раскладка этажей подобраны проектировщиком под габариты помещений брифа; обмер и проект АР — задание (К-1); высота потолка 2900 мм — по брифу, не замерена; перекрытие 330 мм и отметка 2-го этажа +3,230 приняты; проект КР — задание (К-2); наружные стены 400 мм, перегородки 120 мм приняты (в брифе толщин нет) (К-1); разрешённая мощность 15 кВт принята по типовым ТУ для частного дома (К-4); подрайон климата не задан — принят не северный (жилые от 2,5 м) (К-7).

См. лист открытых вопросов (лист 7, записи К-1, К-2, К-4; лист 8, запись К-7).

Изм.	Кол.уч	Лист	№ док.	Подп.	Дата
Разраб.		Кырлан А.С.			04.11.26
Пров.					
ГИП					
Н. контр.					
Утв.					

ГД-2026-012-АИ

Дом 120 м²

Общая площадь 147,36* м² · * размеры приняты, не замерены (реестр — л. 7–9, К-1)

Дизайн-проект интерьера

Стадия	Лист	Листов
РП	12	175

Задание на контрольный обмер и обследование.
Лист 3 из 4
М б/м

Кырлан Александр Сергеевич

выпуск 04.11.2026 № 4dfa962484 · стр. 12 из 180

Задание на контрольный обмер и обследование. Лист 4 из 4

ПРЕДВАРИТЕЛЬНО · не для производства работ · открыто пунктов: 11 (реестр — л. 7–9)

Что замерить, вскрыть и получить до заказа материалов и изделий

Этап 2. После демонтажа, до черновых работ

№	Где	Способ	Что сделать	Кто выполняет	Точность	Что пересчитается в альбоме	Чем подтверждается	Закрывает вопросы реестра
О-20	Гостиная-кухня (пом. 1), Холл с лестницей (пом. 2), Кабинет (пом. 3), Санузел гостевой (пом. 4), Прихожая (пом. 5), Спальня родителей (пом. 6), Детская (пом. 7), Гардеробная (пом. 8), Кладовая (пом. 9), Холл второго этажа (пом. 10), Коридор второго этажа (пом. 11), Детская вторая (пом. 12), Санузел второго этажа (пом. 13)	Обмер	Нивелировка плиты перекрытия и существующего пола после демонтажа покрытий: отметки в углах и по сетке, перепады по помещению, уклоны, отметки порогов (чистый пол в мокрых зонах принят -15 мм, 0 мм). Принятая толщина стяжки 33 мм, 50 мм и отметка чистого пола — расчётные, не от замера плиты.	Архитектор	±5 мм по отметке; ровность просвет под 2-метровой рейкой, горизонталь против 0,2 % длины помещения	Толщина стяжки и отметка чистого пола; уклоны к трапам и пороги; выпуски К1 относительно чистого пола (план разводки); объёмы стяжки и смеси в ВОР и спецификации. Листы: л. 74, 78, 79 — План полов л. 54, 55 — Схема разводки водопровода и канализации	акт контрольного обмера	Вопроса в реестре нет: Альбом принимает отметки плиты и толщину пирога пола без нивелировки. Результат принимает: Отделочник
О-21	Гостиная-кухня (пом. 1), Холл с лестницей (пом. 2), Кабинет (пом. 3), Санузел гостевой (пом. 4), Прихожая (пом. 5), Спальня родителей (пом. 6), Детская (пом. 7), Гардеробная (пом. 8), Кладовая (пом. 9), Холл второго этажа (пом. 10), Коридор второго этажа (пом. 11), Детская вторая (пом. 12), Санузел второго этажа (пом. 13)	Обмер	Вертикаль и плоскостность стен: отклонение от вертикали по высоте стены (отвес или лазерный уровень), просвет под правилом 2 м, кривизна углов. Нужно там, где от стены зависит изделие: облицовка плиткой (пом. 4, 13), штукатурка и окраска (пом. 1, 2, 3, 4, 5, 6, 7, 8, 9, 10, 11, 12, 13), встроенная мебель и кухня (пом. 1, 5, 6, 7, 12).	Архитектор	до 1 мм на 2 м (правило и клиновой щуп); вертикаль — мм на высоту стены, отклонения подписываются на плане	Толщина штукатурки и расход смеси в ВОР и спецификации; раскладка плитки (подрезка у стен); зазоры и крепление встроенной мебели и кухни. Листы: л. 74–77 — Раскладка плитки л. 80–82 — Ведомость отделки помещений	акт контрольного обмера	Вопроса в реестре нет: Альбом принимает стены ровными и вертикальными без замера. Результат принимает: Отделочник

Документы и данные закупки (не на объекте)

№	У кого, откуда	Способ	Что получить	К какому сроку	Что пересчитается в альбоме	Чем подтверждается	Закрывает вопросы реестра
О-22	Заказчик; организация, выдавшая технические условия	Документ	Технические условия на присоединение: разрешённая мощность.	До утверждения однолинейной схемы щита	Однолинейная схема щита: вводной аппарат и группы. Листы: л. 2–6 — Общие данные	копия документа	К-4 Результат принимает: Инженер-электрик
О-23	заказчик	Документ	Проект дома (разделы АР, КР, ВК, ОВ) или обследование: несущие конструкции, перекрытие, стояки, вводы сетей.	до демонтажа и возведения перегородок	монтажный план, проёмы, стояки, развёртки Листы: л. 17, 18 — Обмерный план л. 17–22, 25–28, 34–39, 44–55, 61, 62, 66, 67, 77–79, 83, 84, 89, 90, 96, 97, 116, 117, 155–159, 164–167 — 1-й этаж л. 54, 55 — Схема разводки водопровода и канализации	копия документа	К-5 Результат принимает: Архитектор
О-24	адрес объекта, СП 131.13330	Документ	Климатический подрайон по СП 131.13330 (по адресу объекта)	до заказа каркаса потолков	план потолков, разрезы, ведомость объёмов Листы: л. 66, 67 — План потолков л. 17–22, 25–28, 34–39, 44–55, 61, 62, 66, 67, 77–79, 83, 84, 89, 90, 96, 97, 116, 117, 155–159, 164–167 — 1-й этаж	копия документа	К-7 Результат принимает: Архитектор

Примечания

1. Подтверждение: акт контрольного обмера (дата, кто присутствовал, прибор, перечень промеров с результатами, подписи присутствующих); к акту — фото вскрытий и узлов и техническое заключение организации, выполнившей обследование.
2. Номера листов — по ведомости рабочих чертежей комплекта (лист «Общие данные»).
3. Пункт исключается из задания при следующем выпуске, когда акт подписан, значение внесено в проект и листы перевыпущены; знак «*» у величины снимается только замером.

Допущения и предложения на листе

Основа листа: взаимное расположение помещений, контур дома 9600 × 8000 и раскладка этажей подобраны проектировщиком под габариты помещений брифа; обмер и проект АР — задание (К-1); высота потолка 2900 мм — по брифу, не замерена; перекрытие 330 мм и отметка 2-го этажа +3,230 приняты; проект КР — задание (К-2); наружные стены 400 мм, перегородки 120 мм приняты (в брифе толщин нет) (К-1); разрешённая мощность 15 кВт принята по типовым ТУ для частного дома (К-4); подрайон климата не задан — принят не северный (жилые от 2,5 м) (К-7).

См. лист открытых вопросов (лист 7, записи К-1, К-2, К-4; лист 8, запись К-7).

Изм.	Кол.уч	Лист	№ док.	Подп.	Дата
Разраб.		Кырлан А.С.			04.11.26
Пров.					
ГИП					
Н. контр.					
Утв.					

ГД-2026-012-АИ

Дом 120 м²

Общая площадь 147,36* м² · * размеры приняты, не замерены (реестр — л. 7–9, К-1)

Дизайн-проект интерьера

Стадия	Лист	Листов
РП	13	175

Задание на контрольный обмер и обследование.
Лист 4 из 4
М б/м

Кырлан Александр Сергеевич

График закупок и работ. Лист 1 из 3

ПРЕДВАРИТЕЛЬНО · не для производства работ · открыто пунктов: 11 (реестр — л. 7–9)

Что заказывать и когда не раньше чего: относительный порядок без дат; срок поставки — из данных или «не задан» с записью реестра

Лист не содержит дат: контрольного обмера, подписанных решений автора и договоров ещё нет, и любая дата была бы выдумана. Вместо календаря — порядок и условия: замер → решение и выбор изделия → заказ → срок поставки → работа, которую позиция блокирует.
Срок поставки печатается как срок, только если он задан в данных позиции. Нет — «срок поставки не задан» и ссылка на вопрос реестра о сроках; типовой диапазон практики стоит рядом как ориентир и заказывать по нему нельзя. Номера З-N и Р-N — строки этого листа, К-N — записи реестра открытых вопросов, О-N — позиции задания на контрольный обмер.

Закупки: что заказывается, от чего зависит заказ и какую работу блокирует

№	Позиция и где	1. Замер до заказа	2. Решение, выбор изделия, паспорт	3. Условие заказа	4. Срок поставки	5. Блокирует работу	Закрывает вопросы реестра
З-1	Двери скрытого монтажа с коробом под покраску в существующих проёмах: Д-1, Д-2, Д-3, Д-4, Д-5, Д-6, Д-7, Д-10, Д-9, Д-8 — 10 шт. пом. 1, 3, 4, 5, 6, 7, 8, 9, 12, 13	О-7: обмер: Гостиная-кухня (пом. 1): окно пом. 1, стена А, окно пом. 1, стена А, дверь пом. 1, стена Б (К-1) О-9: обмер: Кабинет (пом. 3): окно пом. 3, стена В, дверь пом. 3, стена Б (К-1) О-10: обмер: Санузел гостевой (пом. 4): дверь пом. 4, стена В (К-1) О-11: обмер: Прихожая (пом. 5): дверь пом. 5, стена В, дверь пом. 5, стена А (К-1) О-12: обмер: Спальня родителей (пом. 6): окно пом. 6, стена А, дверь пом. 6, стена Б (К-1) О-13: обмер: Детская (пом. 7): окно пом. 7, стена В, дверь пом. 7, стена Б (К-1) О-14: обмер: Гардеробная (пом. 8): дверь пом. 8, стена Б (К-1) О-15: обмер: Кладовая (пом. 9): дверь пом. 9, стена Б (К-1) О-18: обмер: Детская вторая (пом. 12): окно пом. 12, стена В, дверь пом. 12, стена А (К-1) О-19: обмер: Санузел второго этажа (пом. 13): дверь пом. 13, стена А (К-1) О-3: обмер: все помещения (К-1); до заказа мебели и дверей		После 1 и 2 и после получения срока у поставщика (вопроса о сроках нет); дата заказа — когда срок известен, не позднее чем за срок до начала Р-5.	срок поставки не задан (записи реестра нет) Ориентир практики (не срок поставщика): ≈ 30 дн.	Р-5 «штукатурка»: короб ставят до штукатурки (коробку ставят на черновой стадии; полотно навешивают после чистовой отделки стен)	К-1
З-2	Кухонный гарнитур по проекту кухни: модули Кх1, Кх2, Кх3, Кх5, Кх6, Кх7, Кх8, Кх9, Кх10, Кх11, Кх12, Кх13, Кх14 пом. 1			После 1 и 2 и после получения срока у поставщика (вопроса о сроках нет); дата заказа — когда срок известен, не позднее чем за срок до начала Р-15.	срок поставки не задан (записи реестра нет) Ориентир практики (не срок поставщика): 4–8 нед. от замера	Р-15 «кухня и мебель»: замер кухни — по готовым стенам после штукатурки или плитки, до чистового пола; производство идёт параллельно со стяжкой и отделкой	
З-3	Встраиваемая техника кухни: Кх3 посудомоечная машина, Кх9 холодильник пом. 1			После 1 и 2 и после получения срока у поставщика (вопроса о сроках нет); дата заказа — когда срок известен, не позднее чем за срок до начала Р-15.	срок поставки не задан (записи реестра нет)	Р-15 «кухня и мебель»: паспорта и монтажные схемы — до изготовления модулей кухни: нишу и вентзазоры задаёт модель, а не типовая схема 60 см	
З-4	Стиральная машина: См3** (вертикальная загрузка 400 × 600 мм — условие закупки) пом. 13			После 1 и 2 и после получения срока у поставщика (вопроса о сроках нет); дата заказа — когда срок известен, не позднее чем за срок до начала Р-4.	срок поставки не задан (записи реестра нет)	Р-4 «черновая сантехника»: габарит и подводка — до закрытия люка и разводки	
З-5	Сантехнические приборы и инсталляции: Ст1, Ст2, См1**, См2**, См4** пом. 4, 13	О-5: обмер: Санузел гостевой (пом. 4): Ст К1-1, Ст В1-1*, Ст Т3-1*; Гостиная-кухня (пом. 1): Ст К1-2 (кухня)*, Ст В1-2*, Ст Т3-2*; наличие стояка ГВС, арматуры и счётчиков — по всей квартире (К-5) О-2: обмер: у окон		После 1 и 2 и после получения срока у поставщика (вопроса о сроках нет); дата заказа — когда срок известен, не позднее чем за срок до начала Р-4.	срок поставки не задан (записи реестра нет)	Р-4 «черновая сантехника»: инсталляцию ставят до обшивки ГКЛВ и до гидроизоляции стены	К-5

Допущения и предложения на листе

Основа листа: взаимное расположение помещений, контур дома 9600 × 8000 и раскладка этажей подобраны проектировщиком под габариты помещений брифа; обмер и проект АР — задание (К-1); высота потолка 2900 мм — по брифу, не замерена; перекрытие 330 мм и отметка 2-го этажа +3,230 приняты; проект КР — задание (К-2); наружные стены 400 мм, перегородки 120 мм приняты (в брифе толщин нет) (К-1); разрешённая мощность 15 кВт принята по типовым ТУ для частного дома (К-4); подрайон климата не задан — принят не северный (жилые от 2,5 м) (К-7).

Знак «*» — принято, не замерено и не подтверждено (замерить на объекте): К-5: Ст В1-1, Ст Т3-1, Ст К1-2 (кухня), Ст В1-2, Ст Т3-2 — положение стояка принято проектировщиком (проект ВК дома не передан), не замерено.

Знак «**» — предложение проектировщика, заказчиком не утверждено (согласовать с заказчиком): ИЗ-1: См1 — Было у стены В offset 150 — заходила в полосу 600 мм перед проёмом Д-8 и в зону 750 перед машиной См3; См2 — Было offset 900…1300 — габарит накрывал стояки Ст К1-1 / В1-1 (у 6570…6700); См3 — Было у стены Г offset 300 — пересекалась с умывальником См4 в углу А/Г, люк упирался в раковину; К-9: См4 — Было offset 500…1100 — пересекалась со стиральной машиной См3.

См. лист открытых вопросов (лист 7, записи К-1, К-2, К-4, К-5; лист 8, записи К-7, К-9; лист 9, запись ИЗ-1).

Изм.	Кол.уч	Лист	№ док.	Подп.	Дата
Разраб.		Кырлан А.С.			04.11.26
Пров.					
ГИП					
Н. контр.					
Утв.					

ГД-2026-012-АИ

Дом 120 м²

Общая площадь 147,36* м² · * размеры приняты, не замерены (реестр — л. 7–9, К-1)

Дизайн-проект интерьера

Стадия	Лист	Листов
РП	14	175

График закупок и работ. Лист 1 из 3

М б/м

Кырлан Александр Сергеевич

выпуск 04.11.2026 № 4dfa962484 · стр. 14 из 180

График закупок и работ. Лист 2 из 3

Что заказывать и когда не раньше чего: относительный порядок без дат; срок поставки — из данных или «не задан» с записью реестра

Закупки: что заказывается, от чего зависит заказ и какую работу блокирует (продолжение)

№	Позиция и где	1. Замер до заказа	2. Решение, выбор изделия, паспорт	3. Условие заказа	4. Срок поставки	5. Блокирует работу	Закрывает вопросы реестра
З-6	Керамогранит и плитка: 3 поз. по артикулу и формату, 61,63 м² по раскладке пом. 1, 4, 5, 13	О-20: обмер: Гостиная-кухня (пом. 1), Холл с лестницей (пом. 2), Кабинет (пом. 3), Санузел гостевой (пом. 4), Прихожая (пом. 5), Спальня родителей (пом. 6), Детская (пом. 7), Гардеробная (пом. 8), Кладовая (пом. 9), Холл второго этажа (пом. 10), Коридор второго этажа (пом. 11), Детская вторая (пом. 12), Санузел второго этажа (пом. 13) О-21: обмер: Гостиная-кухня (пом. 1), Холл с лестницей (пом. 2), Кабинет (пом. 3), Санузел гостевой (пом. 4), Прихожая (пом. 5), Спальня родителей (пом. 6), Детская (пом. 7), Гардеробная (пом. 8), Кладовая (пом. 9), Холл второго этажа (пом. 10), Коридор второго этажа (пом. 11), Детская вторая (пом. 12), Санузел второго этажа (пом. 13)		После 1 и 2 и после получения срока у поставщика (вопроса о сроках нет); дата заказа — когда срок известен, не позднее чем за срок до начала Р-9.	срок поставки не задан (записи реестра нет)	Р-9 «плитка»: калибр партии измеряют до раскладки, раскладку пересчитывают до заказа	
З-7	Покрытие пола (доска) и плинтус: пом. 1, 2, 3, 6, 7, 8, 9, 10, 11, 12 пом. 1, 2, 3, 6, 7, 8, 9, 10, 11, 12	О-20: обмер: Гостиная-кухня (пом. 1), Холл с лестницей (пом. 2), Кабинет (пом. 3), Санузел гостевой (пом. 4), Прихожая (пом. 5), Спальня родителей (пом. 6), Детская (пом. 7), Гардеробная (пом. 8), Кладовая (пом. 9), Холл второго этажа (пом. 10), Коридор второго этажа (пом. 11), Детская вторая (пом. 12), Санузел второго этажа (пом. 13)		После 1 и 2 и после получения срока у поставщика (вопроса о сроках нет); дата заказа — когда срок известен, не позднее чем за срок до начала Р-12.	срок поставки не задан (записи реестра нет)	Р-12 «чистовые полы»: артикул и партия — до заказа; доску привозят к чистовым полам	
З-8	Встроенная мебель по замеру цеха: Пх1, М4, Дт3, Дт8 пом. 5, 6, 7, 12	О-3: обмер: все помещения (К-1); до заказа мебели и дверей		После 1 и 2 и после получения срока у поставщика (вопроса о сроках нет); дата заказа — когда срок известен, не позднее чем за срок до начала Р-15.	срок поставки не задан (записи реестра нет) Ориентир практики (не срок поставщика): 4–8 нед. от замера	Р-15 «кухня и мебель»: цех замеряет по готовым стенам; производство 4–8 недель идёт параллельно с отделкой	К-1

Работы: порядок и что не даёт начать

№	Работа (стадия технологической последовательности)	После	Что должно быть к началу: условия и закупки	Не начинать, пока открыто в реестре
Р-1	Демонтаж покрытий, отделки стен и потолков, дверных блоков и приборов; конструкции, стены и перегородки не трогать до технического заключения (стадия 1)		до начала: запрошены документы на дом и БТИ; контрольный обмер до демонтажа (что видно) сделан	
Р-2	Контрольный обмер на голых стенах и обследование (задание — лист «Задание на контрольный обмер») (стадия 2)	Р-1	после снятия отделки: видны стояки, каналы, щиток, толщины стен; до заказа всего, что делают по размеру	
Р-3	Черновая электрика: штробы, короба, гофра, подрозетники, щит (стадия 4)	Р-2	до начала: план электрики с высотами утверждён; штробы в стенах — только после технического заключения; мебель расставлена	К-4: Разрешённая мощность дома по ТУ неизвестна, принята 15 кВт.

Допущения и предложения на листе

Основа листа: взаимное расположение помещений, контур дома 9600 × 8000 и раскладка этажей подобраны проектировщиком под габариты помещений брифа; обмер и проект АР — задание (К-1); высота потолка 2900 мм — по брифу, не замерена; перекрытие 330 мм и отметка 2-го этажа +3,230 приняты; проект КР — задание (К-2); наружные стены 400 мм, перегородки 120 мм приняты (в брифе толщин нет) (К-1); разрешённая мощность 15 кВт принята по типовым ТУ для частного дома (К-4); подрайон климата не задан — принят не северный (жилые от 2,5 м) (К-7).

См. лист открытых вопросов (лист 7, записи К-1, К-2, К-4; лист 8, запись К-7).

Изм.	Кол.уч	Лист	№ док.	Подп.	Дата
Разраб.		Кырлан А.С.			04.11.26
Пров.					
ГИП					
Н. контр.					
Утв.					

ГД-2026-012-АИ

Дом 120 м²

Общая площадь 147,36* м² · * размеры приняты, не замерены (реестр — л. 7–9, К-1)

Дизайн-проект интерьера

Стадия	Лист	Листов
РП	15	175

График закупок и работ. Лист 2 из 3

М б/м

Кырлан Александр Сергеевич

выпуск 04.11.2026 № 4dfa962484 · стр. 15 из 180

График закупок и работ. Лист 3 из 3

ПРЕДВАРИТЕЛЬНО · не для производства работ · открыто пунктов: 11 (реестр — л. 7–9)

Что заказывать и когда не раньше чего: относительный порядок без дат; срок поставки — из данных или «не задан» с записью реестра

Работы: порядок и что не даёт начать (продолжение)

№	Работа (стадия технологической последовательности)	После	Что должно быть к началу: условия и закупки	Не начинать, пока открыто в реестре
Р-4	Черновая сантехника и вентиляция: разводка, выводы, инсталляции, короба стояков (стадия 5)	Р-2	до начала: положение стояков замерено; модели инсталляций и машины выбраны (габариты рамы, подводка); инсталляцию ставят до обшивки ГКЛВ и до гидроизоляции Закупки к началу: З-4 (стиральная машина), З-5 (сантехника)	К-5: Тип дома, материал и конструкция стен и перекрытия, несущие стены, положение стояков, выпусков канализации и вентканалов в брифе не заданы; проект дома (АР, КР, ВК, ОВ) не передан.
Р-5	Коробки скрытых дверей, затем штукатурка стен и откосов (стадия 6)	Р-2, Р-3, Р-4	до начала: электрика и сантехника смонтированы, штробы заделаны; коробки скрытых дверей установлены до штукатурки (поэтому заказ дверей — раньше работы) Закупки к началу: З-1 (двери скрытого монтажа)	К-1: Бриф задаёт 11 помещений с габаритами и этажами, но не их взаимное расположение, контур дома и толщины стен: раскладка этажей, контур 9600 × 8000 и перегородки подобраны проектировщиком под габариты брифа.
Р-6	Стяжка пола и тёплый пол (стадия 7)	Р-5	до начала: штукатурка сделана; трубы под стяжкой приняты; нивелировка плиты выполнена	
Р-7	Гидроизоляция санузлов и тест проливом (стадия 8)	Р-6	до начала: стяжка набрала прочность и сухая по инструкции гидроизоляции; выводы стоят на проектных отметках	
Р-8	ГКЛ: короба инсталляции и стояков, ниши, потолки (стадия 9)	Р-3, Р-4	до начала: черновые сети в зоне коробов приняты; закладные под тяжёлое и карнизы стоят; светильники выбраны (вырезы)	
Р-9	Плитка и керамогранит: стены, затем пол; фартук (стадия 10)	Р-6, Р-7, Р-8	до начала: гидроизоляция принята; плитка выбрана, калибр партии измерен, раскладка пересчитана и подписана Закупки к началу: З-6 (плитка)	
Р-10	Шпаклёвка стен и потолков под окраску (стадия 11)	Р-5, Р-8, Р-9	до начала: плитка готова (грязные работы закончены); штукатурка и ГКЛ сухие	
Р-11	Окраска стен, потолков, откосов (стадия 13)	Р-10	до начала: шпаклёвка отшлифована и огрунтована; выкрасы утверждены, колеровка одной партией	
Р-12	Чистовые полы: инженерная доска (стадия 14)	Р-9, Р-11	до начала: влажность основания в норме, мокрые работы закончены; доска выбрана и привезена Закупки к началу: З-7 (доска и плинтус)	
Р-13	Полотна межкомнатных дверей, плинтусы, пороги (стадия 15)	Р-11, Р-12	до начала: чистовой пол уложен; полотна скрытых дверей — после чистовой отделки стен	
Р-14	Чистовая электрика и сантехника: механизмы, светильники, смесители, приборы (стадия 16)	Р-11, Р-13	до начала: отделка готова; механизмы, светильники и приборы выбраны и привезены	
Р-15	Кухня, встроенная и корпусная мебель, бытовая техника (стадия 17)	Р-13, Р-14	до начала: чистовая сантехника и электрика подведены к местам мебели; замер кухни снят по готовым стенам (после штукатурки или плитки, до чистового пола) Закупки к началу: З-2 (кухонный гарнитур), З-3 (техника кухни), З-8 (мебель по замеру)	К-1: Бриф задаёт 11 помещений с габаритами и этажами, но не их взаимное расположение, контур дома и толщины стен: раскладка этажей, контур 9600 × 8000 и перегородки подобраны проектировщиком под габариты брифа.
Р-16	Сдача: осмотр по чек-листу, дефектная ведомость, устранение замечаний (стадия 18)	Р-14, Р-15	до начала: всё смонтировано; акты скрытых работ подписаны	

Примечания

1. Порядок работ — стадии технологической последовательности из 16 позиций, присутствующих в этом проекте (по строкам ведомости объёмов); остальные стадии таблицы knowledge/remont-tehnologiya.md в проекте не встречаются. Длительности работ не печатаются: их нет ни в данных, ни в нормах для этого объекта.
2. Типовые сроки — ориентир практики, не срок поставщика: скрытые двери — короб около 10 дн., полотно под покраску до 3 нед., шпон 4–5 нед., в среднем около 30 дн. (knowledge/workers/foreman.md, п. 2.4 (profil-doors)); кухня и корпусная мебель — 4–8 недель от замера (knowledge/remont-tehnologiya.md, разд. 2; knowledge/workers/foreman.md, п. 2.4). Заказ по ориентиру не назначается: срок получают у поставщика (вопрос реестра), после чего заказ планируют «не позднее чем за срок до начала работы».
3. Условия заказа берутся из реестра открытых вопросов и задания на контрольный обмер: позиция заказывается, когда закрыты замер (графа 1) и решение (графа 2). Закрывать их может только факт или решение автора с подписью; снять строку с листа можно только закрыв запись реестра.
4. Заказ по размеру до контрольного обмера не делают: двери, кухня и встроенная мебель зависят от обмера (К-11, К-13); скрытые двери, кроме того, зависят от решения по нише санузла 2 (проём Д-5 в перегородке П-1).
5. Номера листов — по ведомости рабочих чертежей комплекта (лист «Общие данные»).

Допущения и предложения на листе

Основа листа: взаимное расположение помещений, контур дома 9600 × 8000 и раскладка этажей подобраны проектировщиком под габариты помещений брифа; обмер и проект АР — задание (К-1); высота потолка 2900 мм — по брифу, не замерена; перекрытие 330 мм и отметка 2-го этажа +3,230 приняты; проект КР — задание (К-2); наружные стены 400 мм, перегородки 120 мм приняты (в брифе толщин нет) (К-1); разрешённая мощность 15 кВт принята по типовым ТУ для частного дома (К-4); подрайон климата не задан — принят не северный (жилые от 2,5 м) (К-7).

См. лист открытых вопросов (лист 7, записи К-1, К-2, К-4; лист 8, запись К-7).

Изм.	Кол.уч	Лист	№ док.	Подп.	Дата
Разраб.		Кырлан А.С.			04.11.26
Пров.					
ГИП					
Н. контр.					
Утв.					

ГД-2026-012-АИ

Дом 120 м²

Общая площадь 147,36* м² · * размеры приняты, не замерены (реестр — л. 7–9, К-1)

Дизайн-проект интерьера

Стадия	Лист	Листов
РП	16	175

График закупок и работ. Лист 3 из 3

М б/м

Кырлан Александр Сергеевич

выпуск 04.11.2026 № 4dfa962484 · стр. 16 из 180

Обмерный план · 1-й этаж

Существующее положение · размеры в мм · отметки от чистого пола

ПРЕДВАРИТЕЛЬНО · не для производства работ · открыто пунктов: 11 (реестр — л. 7–9)

Экспликация помещений

№	Наименование	Площадь, м²
1	Гостиная-кухня	31,32
2	Холл с лестницей	15,51
3	Кабинет	11,00
4	Санузел гостевой	4,17
5	Прихожая	12,20
	Итого по этажу	**74,20**
	Итого по дому	**147,36**

Условные обозначения

- существующие стены (сечение)
- окно (рама, остекление)
- проём существующий, без заполнения (откосы)
- стояк: К1 — канализация, В1 — ХВС, Т3 — ГВС
- диагональ помещения — контроль прямоугольности
- (1) номер помещения, площадь м²
- * — «*» — принято, не замерено и не подтверждено

Примечания

1. Размеры — в мм по чистым поверхностям стен до отделки (по плану заказчика); площади — в м² по тем же размерам. До начала работ выполнить контрольный обмер.
2. Знак «*» у проёма — положение не замерено; реестр: листы 7–9, вопросы К-1, К-8.
3. За отметку ±0,000 принят чистый пол 1-го этажа, не существующий (блок отметок). «Низ перекрытия» у марки помещения — отметка низа перекрытия от ±0,000, как на развёртках и плане потолков (не высота потолка: потолок — по плану потолков); отметка со знаком «*» — принятая, не замер (вопрос К-2).
4. Толщины стен: наружные 400 мм, перегородки 120 мм; отличающиеся толщины и уступы размерами на плане.
5. Несущие стены не определены: до технического заключения все стены считать несущими; проёмы и штробы в них не выполнять.
6. Дверные проёмы показаны без заполнения (двери — лист 23); высота дверных проёмов 2100 мм; низ окон (подоконник) 500, 900 мм от чистого пола, высота окон 1900, 1500 мм.
7. Диагонали — контрольные размеры; «*» — расчёт по принятому контуру (К-1), при обмере заменить замеренным; расхождение более 5 мм подписать на плане как перекос.
8. Размеры проверить на месте до начала работ; расхождение контрольных промеров ≤ 2 %.

Отметки по высоте


±0,000	чистый пол пом. 1–3, 5; отсчёт высот
−0,015	чистый пол пом. 4, ниже на 15 мм
−0,064*	верх плиты — расчёт, не замер (задание на обмер)
сущ. пол	снимается до плиты; не замерен (задание на обмер)

Принято, не определено или спорно

полностью — листы 7–9

К-3 — Лестница по брифу — из холла 1-го этажа; место, тип (одномаршевая прямая, 17 подъёмов 190 × 250, марш 1000), конструкция и ограждение предложение проектировщика

К-5 — Тип дома, материал и конструкция стен и перекрытия, несущие стены, положение стояков, выпусков канализации и вентканалов в брифе не заданы; проект дома (АР, КР, ВК, ОВ) не передан

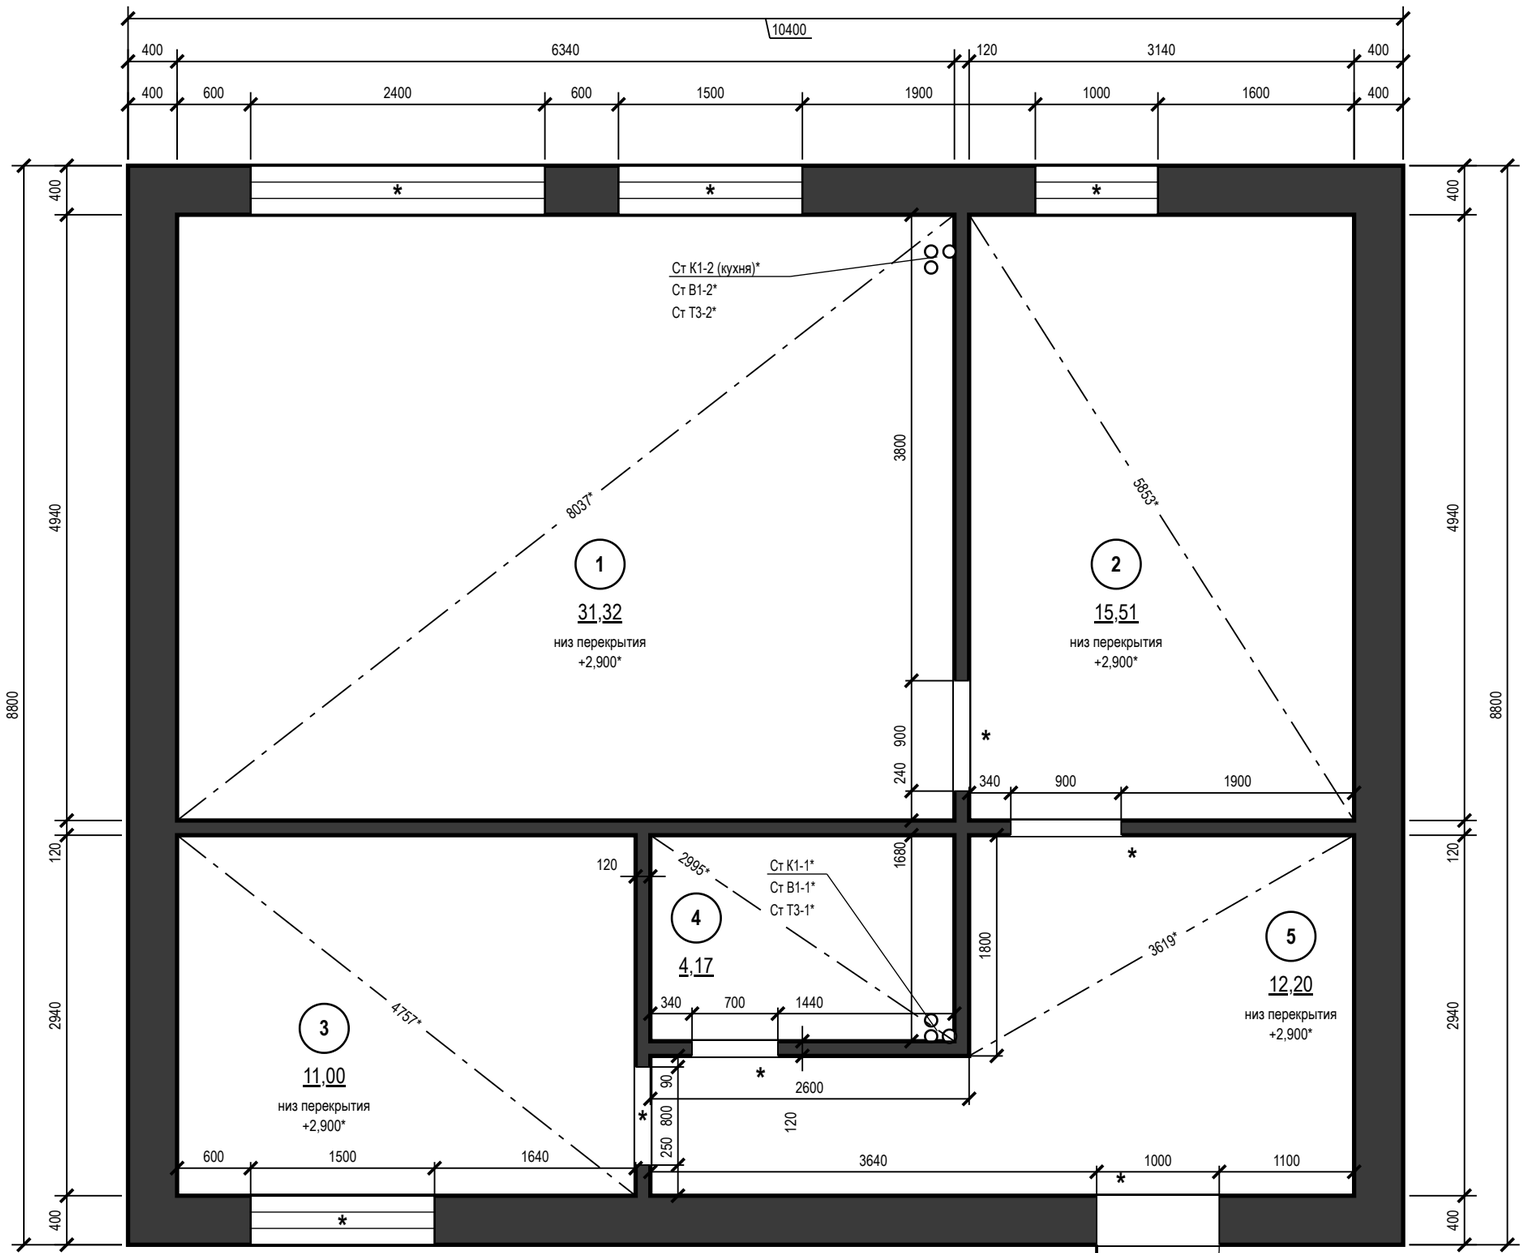

1000 мм · печать 1:1

Допущения и предложения на листе

Основа листа: взаимное расположение помещений, контур дома 9600 × 8000 и раскладка этажей подобраны проектировщиком под габариты помещений брифа; обмер и проект АР — задание (К-1); высота потолка 2900 мм — по брифу, не замерена; перекрытие 330 мм и отметка 2-го этажа +3,230 приняты; проект КР — задание (К-2); наружные стены 400 мм, перегородки 120 мм приняты (в брифе толщин нет) (К-1); разрешённая мощность 15 кВт принята по типовым ТУ для частного дома (К-4); подрайон климата не задан — принят не северный (жилые от 2,5 м) (К-7).

Знак «*» — принято, не замерено и не подтверждено (замерить на объекте): К-1: окно пом. 1 (стена А), 2 (А), 3 (В) — окно: место, ширина, высота и подоконник приняты по брифу, стена — по раскладке проектировщика (К-1), не замерены; дверь пом. 1 (стена Б), 3 (Б), 4 (В), 5 (А) — проём: место и ширина приняты проектировщиком по брифу (раскладка этажей — К-1), не замерены; дверь пом. 5 (стена В) — входная дверь: место и ширина проёма приняты проектировщиком по брифу (без плана дома), не замерены; К-5: Ст К1-1, Ст В1-1, Ст Т3-1, Ст К1-2 (кухня), Ст В1-2, Ст Т3-2 — положение стояка принято проектировщиком (проект ВК дома не передан), не замерено.

Открытые вопросы и конфликты по листу: К-1–К-3, К-5.

См. лист открытых вопросов (лист 7, записи К-1–К-5; лист 8, запись К-7).

Изм.	Кол.уч	Лист	№ док.	Подп.	Дата
Разраб.		Кырлан А.С.			04.11.26
Пров.					
ГИП					
Н. контр.					
Утв.					

ГД-2026-012-АИ

Дом 120 м²

Общая площадь 147,36* м² · * размеры приняты, не замерены (реестр — л. 7–9, К-1)

Дизайн-проект интерьера

Стадия	Лист	Листов
РП	17	175

Обмерный план · 1-й этаж

М 1:50


Кырлан Александр Сергеевич

выпуск 04.11.2026 № 4dfa962484 · стр. 17 из 180

Обмерный план · 2-й этаж

Существующее положение · размеры в мм · отметки от чистого пола

ПРЕДВАРИТЕЛЬНО · не для производства работ · открыто пунктов: 11 (реестр — л. 7–9)

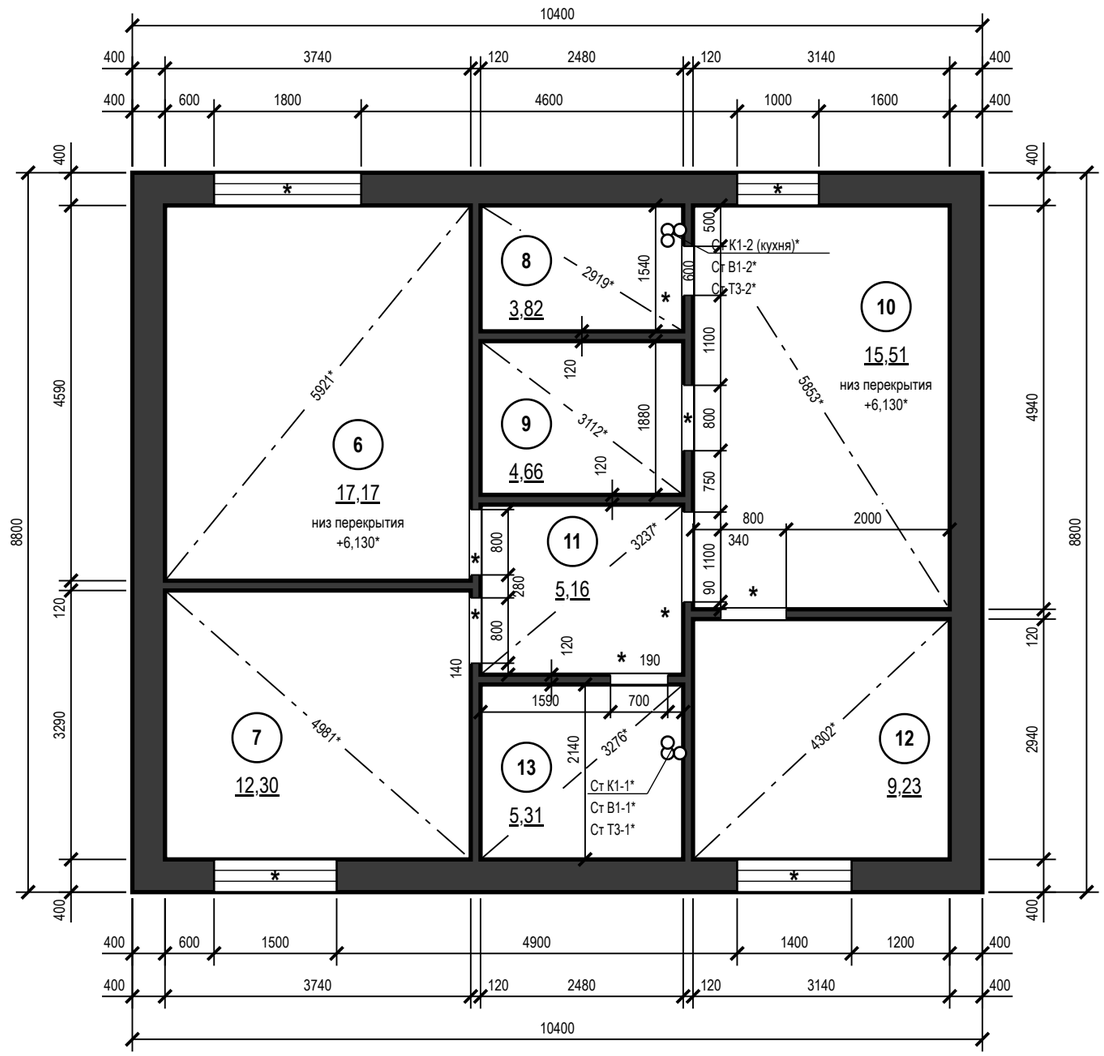

Экспликация помещений

№	Наименование	Площадь, м²
6	Спальня родителей	17,17
7	Детская	12,30
8	Гардеробная	3,82
9	Кладовая	4,66
10	Холл второго этажа	15,51
11	Коридор второго этажа	5,16
12	Детская вторая	9,23
13	Санузел второго этажа	5,31
	Итого по этажу	**73,16**

Условные обозначения

- существующие стены (сечение)
- окно (рама, остекление)
- проём существующий, без заполнения (откосы)
- стояк: К1 — канализация, В1 — ХВС, Т3 — ГВС
- диагональ помещения — контроль прямоугольности
- (1) номер помещения, площадь м²
- * «*» — принято, не замерено и не подтверждено

Примечания

1. Размеры — в мм по чистым поверхностям стен до отделки (по плану заказчика); площади — в м² по тем же размерам. До начала работ выполнить контрольный обмер.
2. Знак «*» у проёма — положение не замерено; реестр: листы 7–9, вопросы К-1, К-9.
3. За отметку ±0,000 принят чистый пол 1-го этажа, не существующий; чистый пол этажа +3,230 (блок отметок). «Низ перекрытия» у марки помещения — отметка низа перекрытия от ±0,000, как на развёртках и плане потолков (не высота потолка: потолок — по плану потолков); отметка со знаком «*» — принятая, не замер (вопрос К-2).
4. Толщины стен: наружные 400 мм, перегородки 120 мм; отличающиеся толщины и уступы размерами на плане.
5. Несущие стены не определены: до технического заключения все стены считать несущими; проёмы и штробы в них не выполнять.
6. Дверные проёмы показаны без заполнения (двери — лист 23); высота дверных проёмов 2100 мм, проёмов без двери 2100 мм; низ окон (подоконник) 900 мм от чистого пола, высота окон 1500, 1450 мм.
7. Диагонали — контрольные размеры; «*» — расчёт по принятому контуру (К-1), при обмере заменить замеренным; расхождение более 5 мм подписать на плане как перекос.
8. Размеры проверить на месте до начала работ; расхождение контрольных промеров ≤ 2 %.
9. Размеры короче 1 мм на листе цепочкой не показаны (две выносные линии на таком расстоянии сливаются): пом. 11, стена Г — 60 мм от угла до проёма.

Отметки по высоте

±0,000	чистый пол 1-го этажа; отсчёт отметок
+3,230*	чистый пол пом. 6–12 (2-й этаж)
+3,215*	чистый пол пом. 13, ниже на 15 мм
+3,166*	верх плиты — расчёт, не замер (задание на обмер)
сущ. пол	снимается до плиты; не замерен (задание на обмер)

Принято, не определено или спорно

полностью — листы 7–9

К-3 — Лестница по брифу — из холла 1-го этажа; место, тип (одномаршевая прямая, 17 подъёмов 190 × 250, марш 1000), конструкция и ограждение предложение проектировщика

К-5 — Тип дома, материал и конструкция стен и перекрытия, несущие стены, положение стояков, выпусков канализации и вентканалов в брифе не заданы; проект дома (АР, КР, ВК, ОВ) не передан

Допущения и предложения на листе. Основа листа: взаимное расположение помещений, контур дома 9600 × 8000 и раскладка этажей подобраны проектировщиком под габариты помещений брифа; обмер и проект АР — задание (К-1); высота потолка 2900 мм — по брифу, не замерена; перекрытие 330 мм и отметка 2-го этажа +3,230 приняты; проект КР — задание (К-2); наружные стены 400 мм, перегородки 120 мм приняты (в брифе толщин нет) (К-1); разрешённая мощность 15 кВт принята по типовым ТУ для частного дома (К-4); подрайон климата не задан — принят не северный (жилые от 2,5 м) (К-7). Знак «*» — принято, не замерено и не подтверждено (замерить на объекте): К-2: отметка чистого пола этажа «2-й этаж» +3,230 — отметка чистого пола 2-го этажа +3,230 принята: высота потолка 2900 по брифу + перекрытие с полом 330 (конструкция перекрытия не задана; проект КР — задание); К-5: Ст К1-1, Ст В1-1, Ст Т3-1, Ст К1-2 (кухня), Ст В1-2, Ст Т3-2 — положение стояка принято проектировщиком (проект ВК дома не передан), не замерено. См. лист открытых вопросов (лист 7, записи К-1–К-5; лист 8, запись К-7); по листу — К-1–К-3, К-5.

1000 мм · печать 1:1

Изм.	Кол.уч	Лист	№ док.	Подп.	Дата
Разраб.		Кырлан А.С.			04.11.26
Пров.					
ГИП					
Н. контр.					
Утв.					

ГД-2026-012-АИ

Дом 120 м²

Общая площадь 147,36* м² · * размеры приняты, не замерены (реестр — л. 7–9, К-1)

Дизайн-проект интерьера

Стадия	Лист	Листов
РП	18	175

Обмерный план · 2-й этаж

М 1:75

Кырлан Александр Сергеевич

выпуск 04.11.2026 № 4dfa962484 · стр. 18 из 180

План демонтажа и монтажа перегородок · 1-й этаж

Перепланировка не выполняется · существующие стены сохраняются · размеры в мм


ПРЕДВАРИТЕЛЬНО · не для производства работ · открыто пунктов: 11 (реестр — л. 7–9)

Условные обозначения

- существующие стены — сохраняются;
- несущие не определены — считать несущими
- демонтируемые конструкции — на плане нет
- возводимые перегородки — на плане нет
- проём существующий, без заполнения (откосы)
- 1 — номер помещения, площадь м²
- * — «*» — принято, не замерено и не подтверждено

Примечания

1. Перепланировка не выполняется: несущие и ненесущие стены, перегородки и плиты перекрытия не демонтируются, новые стены не возводятся; существующие стены и перегородки сохраняются.
2. Дверные блоки — по плану дверей; существующие проёмы не расширяются.
3. Знак «*» — положение проёма не замерено: окна пом. 1, 1, 2, 3; двери пом. 1, 3, 4, 5, 5. Реестр: листы 7–9, вопросы К-1, К-8.
4. Демонтаж существующих покрытий пола, стен и потолка, дверных блоков и сантехприборов (если есть) — до основания; объёмы демонтажа — для справки, по факту на объекте.
5. За отметку ±0,000 принят чистый пол 1-го этажа, не существующий (блок отметок). Размеры — в мм по чистовой поверхности стен до отделки.
6. Размеры проверить на месте до начала работ: расхождение с обмером — не более 2 % (иначе — к архитектору).
7. Несущие стены не определены: до технического заключения все стены считать несущими — проёмы, ниши и штробы в них не выполнять.

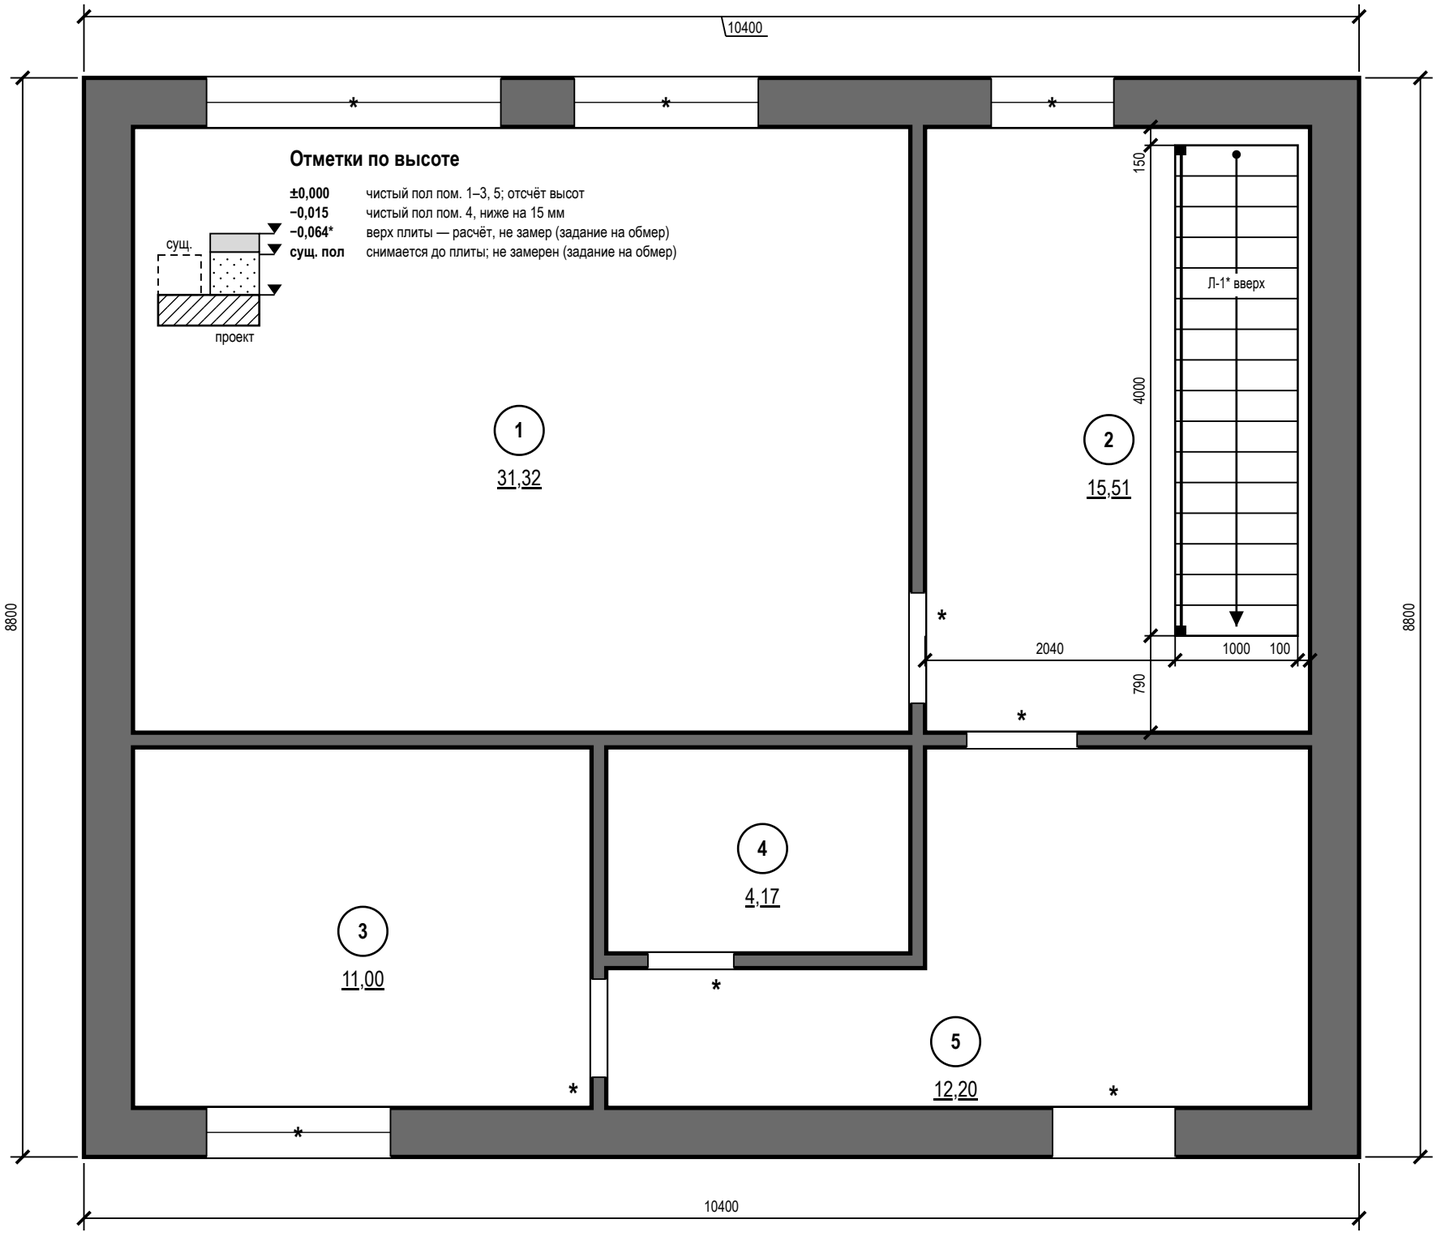

Допущения и предложения на листе

Основа листа: взаимное расположение помещений, контур дома 9600 × 8000 и раскладка этажей подобраны проектировщиком под габариты помещений брифа; обмер и проект АР — задание (К-1); высота потолка 2900 мм — по брифу, не замерена; перекрытие 330 мм и отметка 2-го этажа +3,230 приняты; проект КР — задание (К-2); наружные стены 400 мм, перегородки 120 мм приняты (в брифе толщин нет) (К-1); разрешённая мощность 15 кВт принята по типовым ТУ для частного дома (К-4); подрайон климата не задан — принят не северный (жилые от 2,5 м) (К-7).

Знак «*» — принято, не замерено и не подтверждено (замерить на объекте): К-1: окно пом. 1 (стена А), 2 (А), 3 (В) — окно: место, ширина, высота и подоконник приняты по брифу, стена — по раскладке проектировщика (К-1), не замерены; дверь пом. 1 (стена Б), 3 (Б), 4 (В), 5 (А) — проём: место и ширина приняты проектировщиком по брифу (раскладка этажей — К-1), не замерены; дверь пом. 5 (стена В) — входная дверь: место и ширина проёма приняты проектировщиком по брифу (без плана дома), не замерены; К-3: Л-1 — место, тип и размеры лестницы брифом не заданы (только «лестница из холла 1-го этажа»): одномаршевая 17 × 190 × 250 вдоль стены Б холла — предложение проектировщика; конструкция и расчёт — проект КР.

См. лист открытых вопросов (лист 7, записи К-1–К-4; лист 8, запись К-7).

1000 мм · печать 1:1

Изм.	Кол.уч	Лист	№ док.	Подп.	Дата
Разраб.		Кырлан А.С.			04.11.26
Пров.					
ГИП					
Н. контр.					
Утв.					

ГД-2026-012-АИ

Дом 120 м²

Общая площадь 147,36* м² · * размеры приняты, не замерены (реестр — л. 7–9, К-1)

Дизайн-проект интерьера

Стадия	Лист	Листов
РП	19	175

План демонтажа и монтажа перегородок · 1-й этаж

М 1:50

Кырлан Александр Сергеевич

выпуск 04.11.2026 № 4dfa962484 · стр. 19 из 180

План демонтажа и монтажа перегородок · 2-й этаж

Перепланировка не выполняется · существующие стены сохраняются · размеры в мм

ПРЕДВАРИТЕЛЬНО · не для производства работ · открыто пунктов: 11 (реестр — л. 7–9)

Условные обозначения


- существующие стены — сохраняются;
- несущие не определены — считать несущими
- демонтируемые конструкции — на плане нет
- возводимые перегородки — на плане нет
- проём существующий, без заполнения (откосы)
- 1 — номер помещения, площадь м²
- * — «*» — принято, не замерено и не подтверждено


Примечания

1. Перепланировка не выполняется: несущие и ненесущие стены, перегородки и плиты перекрытия не демонтируются, новые стены не возводятся; существующие стены и перегородки сохраняются.
2. Дверные блоки — по плану дверей; существующие проёмы не расширяются.
3. Знак «*» — положение проёма не замерено: окна пом. 6, 7, 10, 12; двери пом. 6, 7, 8, 9, 11, 12, 13. Реестр: листы 7–9, вопросы К-1, К-9.
4. Демонтаж существующих покрытий пола, стен и потолка, дверных блоков и сантехприборов (если есть) — до основания; объёмы демонтажа — для справки, по факту на объекте.
5. За отметку ±0,000 принят чистый пол 1-го этажа, не существующий; чистый пол этажа +3,230 (блок отметок). Размеры — в мм по чистовой поверхности стен до отделки.
6. Размеры проверить на месте до начала работ: расхождение с обмером — не более 2 % (иначе — к архитектору).
7. Несущие стены не определены: до технического заключения все стены считать несущими — проёмы, ниши и штробы в них не выполнять.

Отметки по высоте

±0,000	чистый пол 1-го этажа; отсчёт отметок
+3,230*	чистый пол пом. 6–12 (2-й этаж)
+3,215*	чистый пол пом. 13, ниже на 15 мм
+3,166*	верх плиты — расчёт, не замер (задание на обмер)
сущ. пол	снимается до плиты; не замерен (задание на обмер)

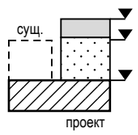

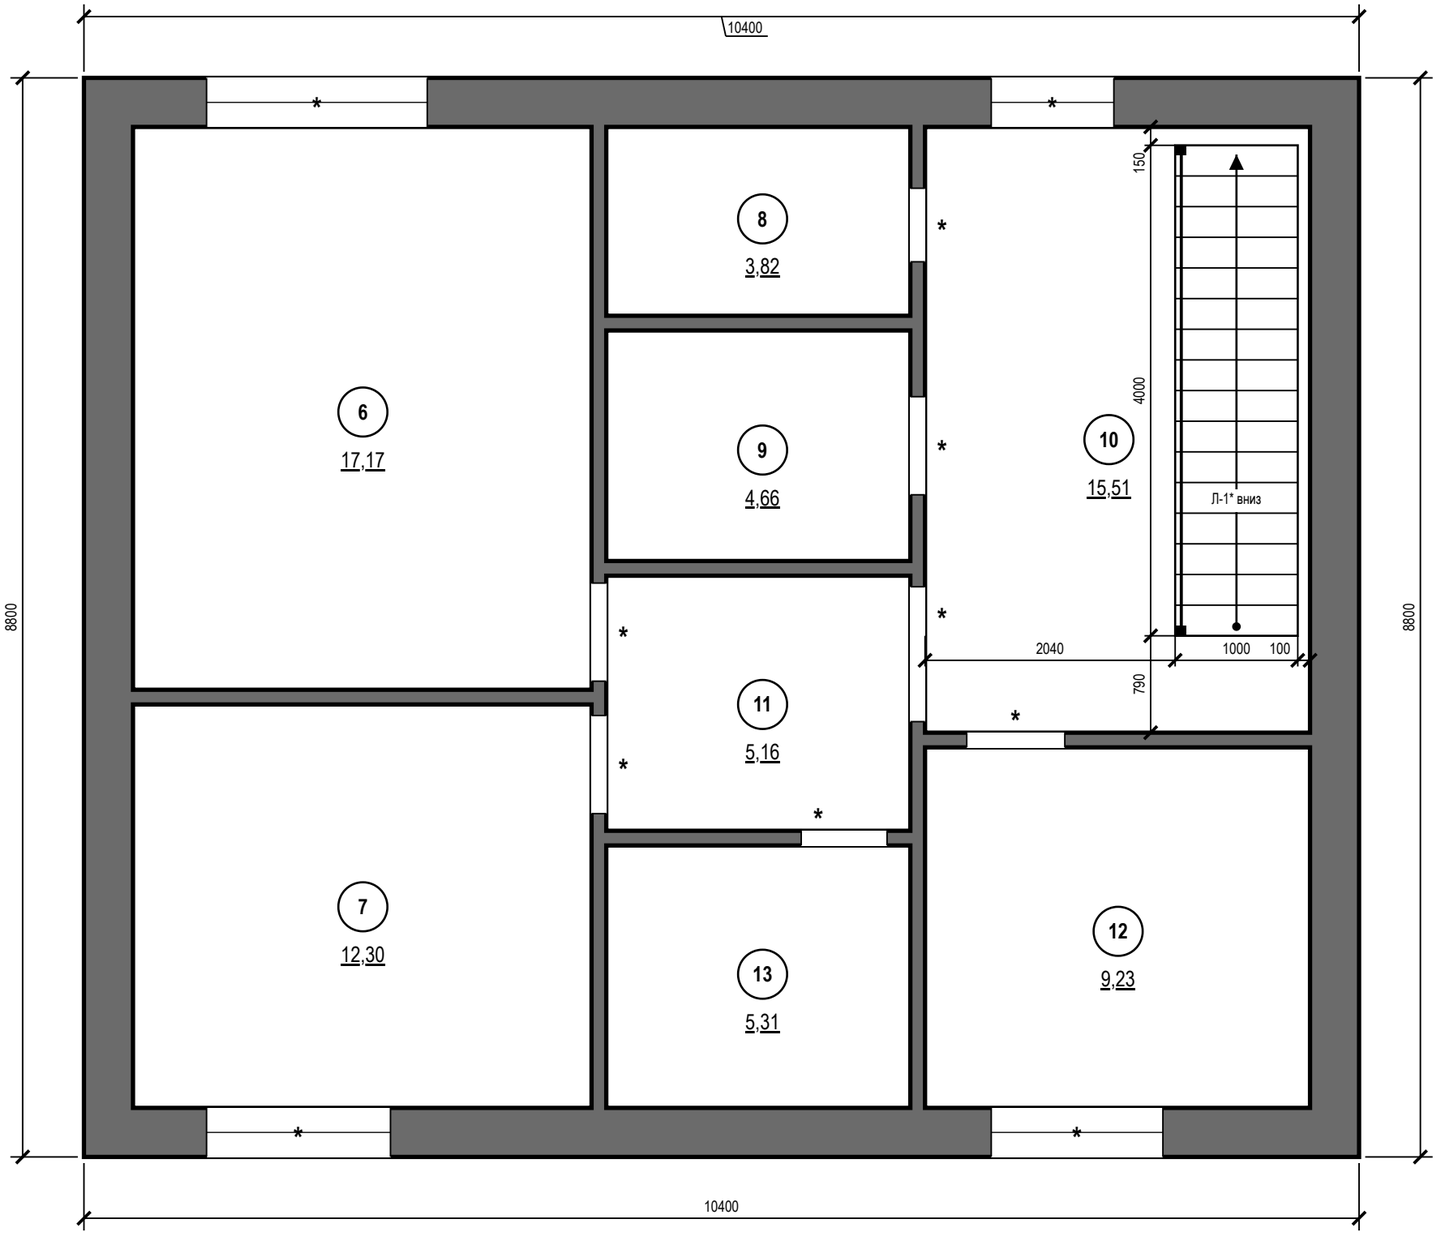

Допущения и предложения на листе

Основа листа: взаимное расположение помещений, контур дома 9600 × 8000 и раскладка этажей подобраны проектировщиком под габариты помещений брифа; обмер и проект АР — задание (К-1); высота потолка 2900 мм — по брифу, не замерена; перекрытие 330 мм и отметка 2-го этажа +3,230 приняты; проект КР — задание (К-2); наружные стены 400 мм, перегородки 120 мм приняты (в брифе толщин нет) (К-1); разрешённая мощность 15 кВт принята по типовым ТУ для частного дома (К-4); подрайон климата не задан — принят не северный (жилые от 2,5 м) (К-7).

Знак «*» — принято, не замерено и не подтверждено (замерить на объекте): К-1: окно пом. 6 (стена А), 7 (В), 10 (А), 12 (В) — окно: место, ширина, высота и подоконник приняты по брифу, стена — по раскладке проектировщика (К-1), не замерены; дверь пом. 6 (стена Б), 7 (Б), 8 (Б), 9 (Б), 11 (Б), 12 (А) — проём: место и ширина приняты проектировщиком по брифу (раскладка этажей — К-1), не замерены; дверь пом. 13 (стена А) — Петли у правого откоса (х 6150, у стояков): открытое полотно стоит вдоль стены Б, вошедший идёт влево к умывальнику и ванне; К-2: отметка чистого пола этажа «2-й этаж» +3,230 — отметка чистого пола 2-го этажа +3,230 принята: высота потолка 2900 по брифу + перекрытие с полом 330 (конструкция перекрытия не задана; проект КР — задание); К-3: Л-1 — место, тип и размеры лестницы брифом не заданы (только «лестница из холла 1-го этажа»): одномаршевая 17 × 190 × 250 вдоль стены Б холла — предложение проектировщика; конструкция и расчёт — проект КР.

См. лист открытых вопросов (лист 7, записи К-1–К-4; лист 8, запись К-7).

1000 мм · печать 1:1

Изм.	Кол.уч	Лист	№ док.	Подп.	Дата
Разраб.		Кырлан А.С.			04.11.26
Пров.					
ГИП					
Н. контр.					
Утв.					

ГД-2026-012-АИ

Дом 120 м²

Общая площадь 147,36* м² · * размеры приняты, не замерены (реестр — л. 7–9, К-1)

Дизайн-проект интерьера

Стадия	Лист	Листов
РП	20	175

План демонтажа и монтажа перегородок · 2-й этаж


М 1:50

Кырлан Александр Сергеевич

выпуск 04.11.2026 № 4dfa962484 · стр. 20 из 180

План дверей · 1-й этаж

Проёмы, марки заполнения, привязки · размеры в мм

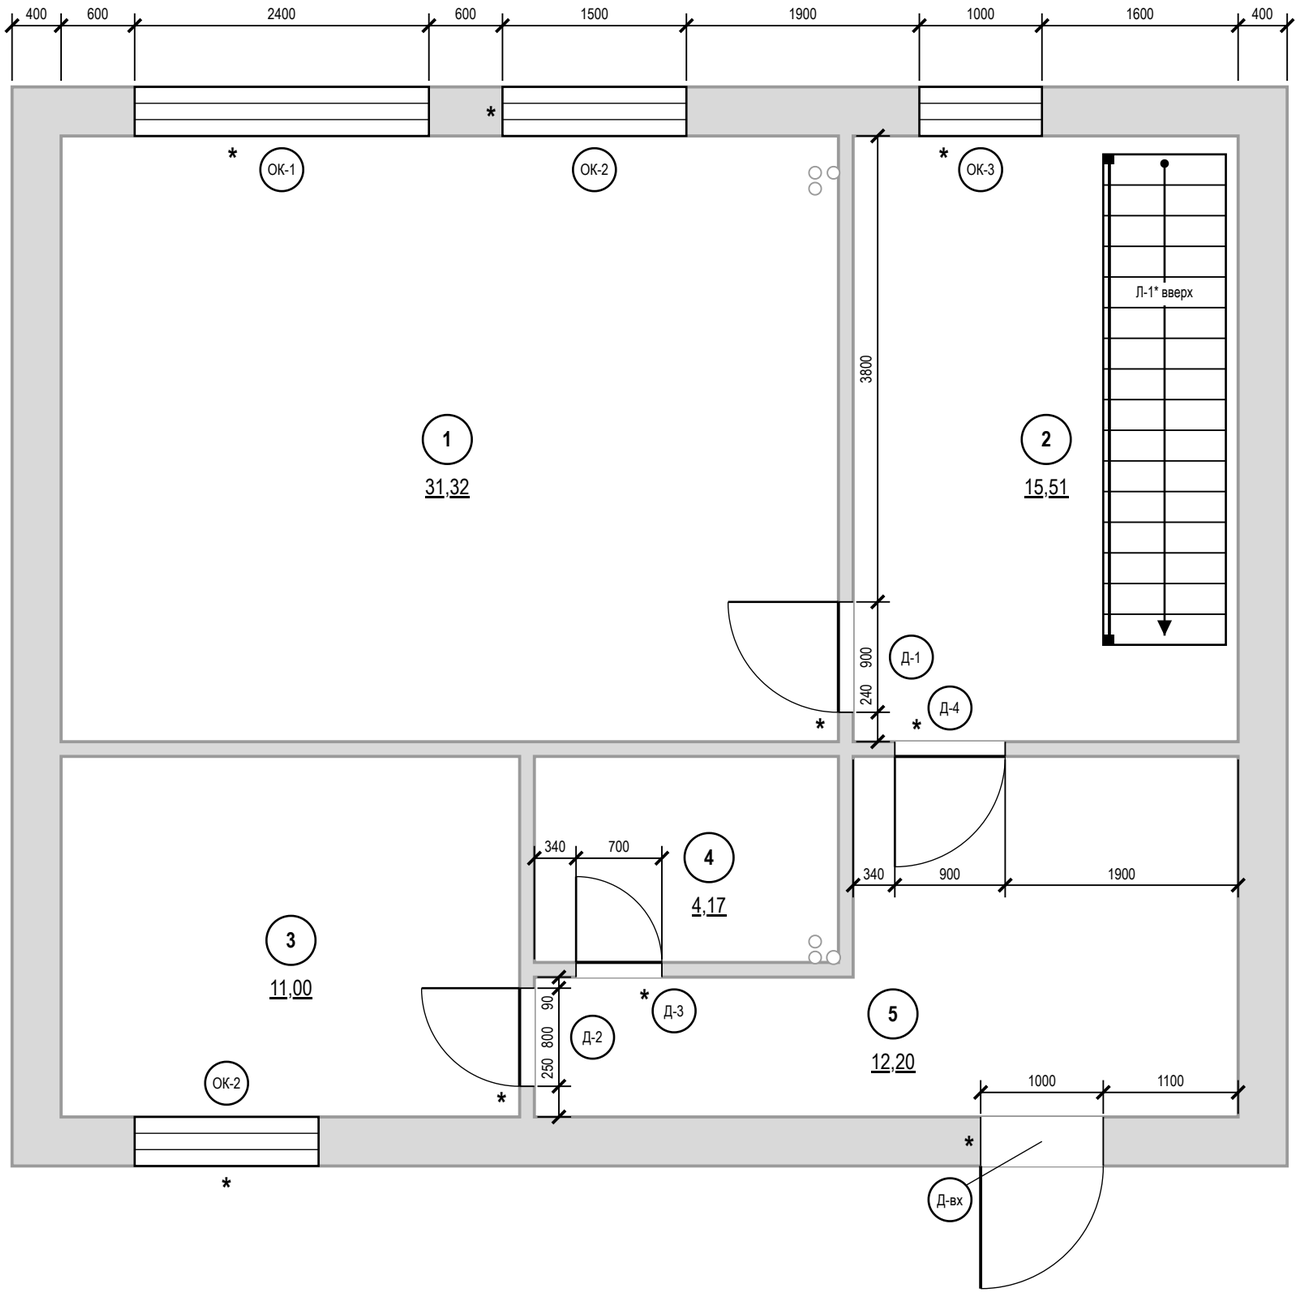

Условные обозначения

- стены (подложка обмера)
- дверь распашная, дуга открывания
- дверь скрытого монтажа
- дверь входная (полотно толще)
- оконный блок
- (Д) марка типа (Д-N, ПР-N, ОК-N)
- (1) номер помещения, площадь м²
- * «*» — принято, не замерено и не подтверждено

Примечания

1. Размеры проёмов и привязки — в миллиметрах от чистых граней стен до отделки; привязка — от угла того помещения, со стороны которого стоит размер. Размер проёма — ширина × высота от чистого пола 0,000. Размеры на плане — проёмов, не полотен: полотно — в ведомости, коробка — по системе. Откос от угла помещения до проёма с коробкой — не менее 50 мм.
2. Марки в кружках — типы заполнения проёмов (ГОСТ 21.501-2018, п. 5.3.2); одна марка — один типоразмер; количество сверено с планом.
3. Д-1…Д-4 — существующие проёмы, до техзаключения не расширять (К-1).
4. Д-вх: дуга наружу — по плану заказчика, не проверено; блок оставить или заменить — не решено (К-1).
5. Знак «*» у проёма — допущение: положение проёма не замерено (окно пом. 1, стена А (2 шт.); дверь пом. 1, стена Б; окно пом. 2, стена А; окно пом. 3, стена В; дверь пом. 3, стена Б; дверь пом. 4, стена В; и ещё 2); размер напечатан как принятый; в ведомости — знак «*» в графе «Прим.». Реестр: листы 7–9, вопросы К-1, К-8.
6. Ведомость заполнения проёмов, открывание полотен, заказ и порядок монтажа блоков — лист 23.

Допущения и предложения на листе

Основа листа: взаимное расположение помещений, контур дома 9600 × 8000 и раскладка этажей подобраны проектировщиком под габариты помещений брифа; обмер и проект АР — задание (К-1); высота потолка 2900 мм — по брифу, не замерена; перекрытие 330 мм и отметка 2-го этажа +3,230 приняты; проект КР — задание (К-2); наружные стены 400 мм, перегородки 120 мм приняты (в брифе толщин нет) (К-1); разрешённая мощность 15 кВт принята по типовым ТУ для частного дома (К-4); подрайон климата не задан — принят не северный (жилые от 2,5 м) (К-7).

Знак «*» — принято, не замерено и не подтверждено (замерить на объекте): К-1: окно пом. 1 (стена А), 2 (А), 3 (В) — окно: место, ширина, высота и подоконник приняты по брифу, стена — по раскладке проектировщика (К-1), не замерены; дверь пом. 1 (стена Б), 3 (Б), 4 (В), 5 (А) — проём: место и ширина приняты проектировщиком по брифу (раскладка этажей — К-1), не замерены; дверь пом. 5 (стена В) — входная дверь: место и ширина проёма приняты проектировщиком по брифу (без плана дома), не замерены; К-3: Л-1 — место, тип и размеры лестницы брифом не заданы (только «лестница из холла 1-го этажа»): одномаршевая 17 × 190 × 250 вдоль стены Б холла — предложение проектировщика; конструкция и расчёт — проект КР; К-5: Ст К1-1, Ст В1-1, Ст Т3-1, Ст К1-2 (кухня), Ст В1-2, Ст Т3-2 — положение стояка принято проектировщиком (проект ВК дома не передан), не замерено.

Изменения по листу без подписи: ИЗ-1.

См. лист открытых вопросов (лист 7, записи К-1–К-5; лист 8, запись К-7; лист 9, запись ИЗ-1).

1000 мм · печать 1:1

Изм.	Кол.уч	Лист	№ док.	Подп.	Дата
Разраб.		Кырлан А.С.			04.11.26
Пров.					
ГИП					
Н. контр.					
Утв.					

ГД-2026-012-АИ

Дом 120 м²

Общая площадь 147,36* м² · * размеры приняты, не замерены (реестр — л. 7–9, К-1)

Дизайн-проект интерьера

Стадия	Лист	Листов
РП	21	175

План дверей · 1-й этаж


М 1:50

Кырлан Александр Сергеевич

выпуск 04.11.2026 № 4dfa962484 · стр. 21 из 180

План дверей · 2-й этаж

Проёмы, марки заполнения, привязки · размеры в мм

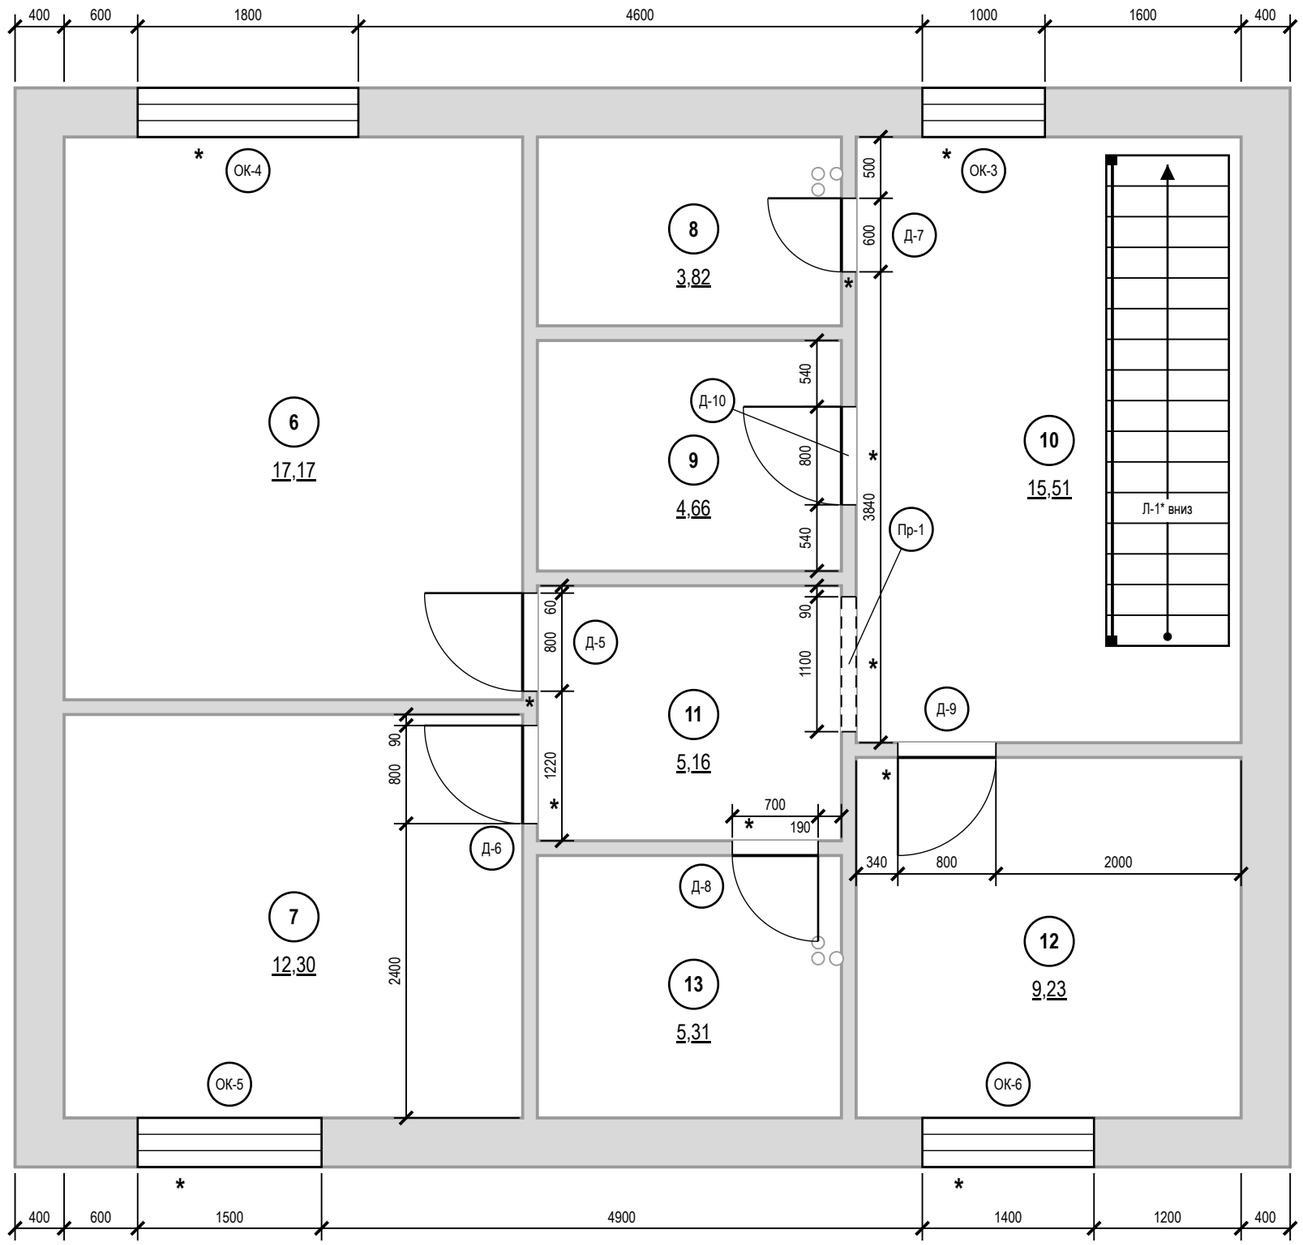

Условные обозначения

- стены (подложка обмера)
- дверь распашная, дуга открывания
- дверь скрытого монтажа
- портал (штрих — перемычка)
- оконный блок
- Д — марка типа (Д-N, ПР-N, ОК-N)
- 1 — номер помещения, площадь м²
- * — «*» — принято, не замерено и не подтверждено

Примечания

1. Размеры проёмов и привязки — в миллиметрах от чистых граней стен до отделки; привязка — от угла того помещения, со стороны которого стоит размер. Размер проёма — ширина × высота от чистого пола 0,000. Размеры на плане — проёмов, не полотен: полотно — в ведомости, коробка — по системе. Откос от угла помещения до проёма с коробкой — не менее 50 мм.
2. Марки в кружках — типы заполнения проёмов (ГОСТ 21.501-2018, п. 5.3.2); одна марка — один типоразмер; количество сверено с планом.
3. Д-5…Д-10 — существующие проёмы, до техзаключения не расширять (К-1).
4. Знак «*» у проёма — допущение: положение проёма не замерено (окно пом. 6, стена А; дверь пом. 6, стена Б; окно пом. 7, стена В; дверь пом. 7, стена Б; дверь пом. 8, стена Б; дверь пом. 9, стена Б; и ещё 5); размер напечатан как принятый; в ведомости — знак «*» в графе «Прим.». Реестр: листы 7–9, вопросы К-1, К-9.
5. Ведомость заполнения проёмов, открывание полотен, заказ и порядок монтажа блоков — лист 23.

Допущения и предложения на листе

Основа листа: взаимное расположение помещений, контур дома 9600 × 8000 и раскладка этажей подобраны проектировщиком под габариты помещений брифа; обмер и проект АР — задание (К-1); высота потолка 2900 мм — по брифу, не замерена; перекрытие 330 мм и отметка 2-го этажа +3,230 приняты; проект КР — задание (К-2); наружные стены 400 мм, перегородки 120 мм приняты (в брифе толщин нет) (К-1); разрешённая мощность 15 кВт принята по типовым ТУ для частного дома (К-4); подрайон климата не задан — принят не северный (жилые от 2,5 м) (К-7).
Знак «*» — принято, не замерено и не подтверждено (замерить на объекте): К-1: окно пом. 6 (стена А), 7 (В), 10 (А), 12 (В) — окно: место, ширина, высота и подоконник приняты по брифу, стена — по раскладке проектировщика (К-1), не замерены; дверь пом. 6 (стена Б), 7 (Б), 8 (Б), 9 (Б), 11 (Б), 12 (А) — проём: место и ширина приняты проектировщиком по брифу (раскладка этажей — К-1), не замерены; дверь пом. 13 (стена А) — Петли у правого откоса (х 6150, у стояков): открытое полотно стоит вдоль стены Б, вошедший идёт влево к умывальнику и ванне; К-2: отметка чистого пола этажа «2-й этаж» +3,230 — отметка чистого пола 2-го этажа +3,230 принята: высота потолка 2900 по брифу + перекрытие с полом 330 (конструкция перекрытия не задана; проект КР — задание); К-3: Л-1 — место, тип и размеры лестницы брифом не заданы (только «лестница из холла 1-го этажа»): одномаршевая 17 × 190 × 250 вдоль стены Б холла — предложение проектировщика; конструкция и расчёт — проект КР; К-5: Ст К1-1, Ст В1-1, Ст Т3-1, Ст К1-2 (кухня), Ст В1-2, Ст Т3-2 — положение стояка принято проектировщиком (проект ВК дома не передан), не замерено.
Изменения по листу без подписи: ИЗ-1.
См. лист открытых вопросов (лист 7, записи К-1–К-5; лист 8, запись К-7; лист 9, запись ИЗ-1).

1000 мм · печать 1:1

Изм.	Кол.уч	Лист	№ док.	Подп.	Дата
Разраб.		Кырлан А.С.			04.11.26
Пров.					
ГИП					
Н. контр.					
Утв.					

ГД-2026-012-АИ

Дом 120 м²

Общая площадь 147,36* м² · * размеры приняты, не замерены (реестр — л. 7–9, К-1)

Дизайн-проект интерьера

Стадия	Лист	Листов
РП	22	175

План дверей · 2-й этаж

М 1:50

Кырлан Александр Сергеевич

выпуск 04.11.2026 № 4dfa962484 · стр. 22 из 180


Ведомость заполнения проёмов

Проёмы, полотна, отделка, фурнитура · размеры в мм


Ведомость заполнения проёмов

Марка	Наименование, обозначение	Проём ш×в, мм	Полотно (расч.)	Кол.	Откр.	Отделка полотна	Фурнитура	Прим.
Д-вх	Блок дверной входной, ГОСТ 31173-2016	1000×2100	блок задать	1	Л	в комплекте блока	в комплекте блока (замки, глазок)	* пом. 5; наружу
Д-1	Дверь скрытого монтажа, UNION FILO-60 Piatto	900×2100	800×2000	1	Л	окраска G503 с двух сторон	скрытые петли 3D, магнитный замок	* пом. 1
Д-2	Дверь скрытого монтажа, UNION FILO-60 Piatto	800×2100	700×2000	1	Л	окраска G503 с двух сторон	скрытые петли 3D, магнитный замок	* пом. 3
Д-3	Дверь скрытого монтажа, UNION FILO-60 Piatto	700×2100	600×2000	1	П	в тон облицовки — пом. 4, G503 — пом. 5	скрытые петли 3D, магнитный замок, фиксатор WC	* пом. 4; порог 15
Д-4	Дверь скрытого монтажа, UNION FILO-60 Piatto	900×2100	800×2000	1	Л	окраска G503 с двух сторон	скрытые петли 3D, магнитный замок	* пом. 5
Д-5	Дверь скрытого монтажа, UNION FILO-60 Piatto	800×2100	700×2000	1	Л	окраска G503 с двух сторон	скрытые петли 3D, магнитный замок	* пом. 6
Д-6	Дверь скрытого монтажа, UNION FILO-60 Piatto	800×2100	700×2000	1	Л	окраска G503 с двух сторон	скрытые петли 3D, магнитный замок	* пом. 7
Д-7	Дверь скрытого монтажа, UNION FILO-60 Piatto	600×2100	не задано (записи реестра нет)	1	Л	No. 222 — пом. 8, G503 — пом. 10	скрытые петли 3D, магнитный замок	* пом. 8
Д-8	Дверь скрытого монтажа, UNION FILO-60 Piatto	700×2100	600×2000	1	П	в тон облицовки — пом. 13, G503 — пом. 11	скрытые петли 3D, магнитный замок, фиксатор WC	* пом. 13; порог 15
Д-9	Дверь скрытого монтажа, UNION FILO-60 Piatto	800×2100	700×2000	1	Л	окраска G503 с двух сторон	скрытые петли 3D, магнитный замок	* пом. 12
Д-10	Дверь скрытого монтажа, UNION FILO-60 Piatto	800×2100	700×2000	1	Л	S 0502-Y — пом. 9, G503 — пом. 10	скрытые петли 3D, магнитный замок	* пом. 9
Пр-1	Портал без заполнения	1100×2100		1				* пом. 11; б/п
ОК-1	Блок оконный, ГОСТ 23166-2021; стекло — триплекс	2400×1900		1				* пом. 1; низ 500
ОК-2	Блок оконный, ГОСТ 23166-2021	1500×1500		2				* пом. 1, 3; низ 900
ОК-3	Блок оконный, ГОСТ 23166-2021	1000×1500		2				* пом. 2, 10; низ 900
ОК-4	Блок оконный, ГОСТ 23166-2021	1800×1500		1				* пом. 6; низ 900
ОК-5	Блок оконный, ГОСТ 23166-2021	1500×1450		1				* пом. 7; низ 900
ОК-6	Блок оконный, ГОСТ 23166-2021	1400×1450		1				* пом. 12; низ 900


Схемы дверных блоков (1:75) — вид со стороны открывания; вершина треугольника — сторона петель

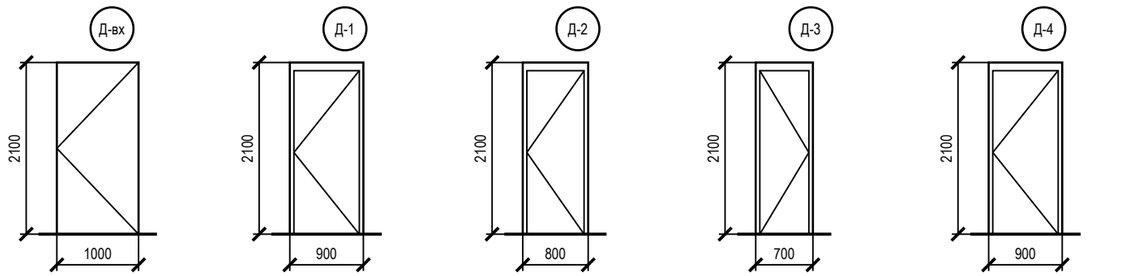

блок — по ГОСТ 31173, откр. Л | полотно 800×2000 (расч.), откр. Л | полотно 700×2000 (расч.), откр. Л | полотно 600×2000 (расч.), откр. П | полотно 800×2000 (расч.), откр. Л

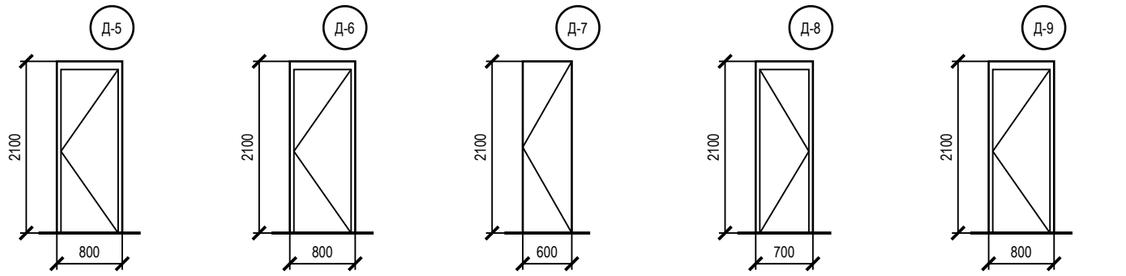

полотно 700×2000 (расч.), откр. Л | полотно 700×2000 (расч.), откр. Л | полотно не задано (записи реестра нет), откр. Л | полотно 600×2000 (расч.), откр. П | полотно 700×2000 (расч.), откр. Л

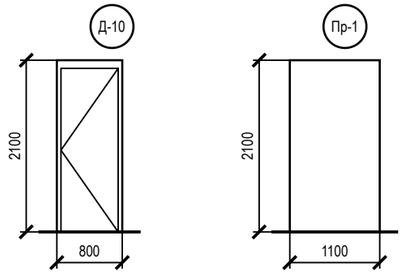

полотно 700×2000 (расч.), откр. Л | без заполнения

Допущения и предложения на листе

Основа листа: взаимное расположение помещений, контур дома 9600 × 8000 и раскладка этажей подобраны проектировщиком под габариты помещений брифа; обмер и проект АР — задание (К-1); высота потолка 2900 мм — по брифу, не замерена; перекрытие 330 мм и отметка 2-го этажа +3,230 приняты; проект КР — задание (К-2); наружные стены 400 мм, перегородки 120 мм приняты (в брифе толщин нет) (К-1); разрешённая мощность 15 кВт принята по типовым ТУ для частного дома (К-4); подрайон климата не задан — принят не северный (жилые от 2,5 м) (К-7). См. лист открытых вопросов (лист 7, записи К-1, К-2, К-4; лист 8, запись К-7).

Примечания

1. Марки проёмов — те же, что на планах дверей этажей (листы 21, 22); привязки проёмов — там же; количество — по всем этажам дома.
2. Открывание: Л — петли слева, П — справа, если смотреть со стороны, куда открывается полотно (на себя).
3. Остекление окон: ОК-1 (пом. 1) — триплекс. Тип стекла указать при заказе оконных блоков; замена на другое стекло — только по согласованию с автором проекта.
4. ОК-1: низ остекления 500 мм — ниже 900 мм от чистого пола, поэтому окно заказывать с безопасным стеклом (триплекс); ограждение проёма в проекте не задано (СП 54.13330.2022, п. 6.4.9; ГОСТ Р 56926).
5. Скрытые двери (Д-1…Д-10): проём замерить в чистоте; блок заказать до штукатурки (≈ 30 дн.), короб ставить до штукатурки; полотно навесить после чистовой отделки, красить в цвет стен. Порядок — практика монтажа, изготовитель подтверждает.
6. Полотно «расч.» — по проёму и ряду изделия с запасом по каталогам, заказ — по таблице проёмов модели; Д-1…Д-6, Д-8…Д-10: проём 2100, а под полотно 2000 по каталогам нужен 2050–2080, под 2100 — 2150–2180: высоту проёма — по модели; Д-вх: входной блок по ГОСТ 31173-2016 — задать при выборе блока; Д-7: проём 600×2100 вне ряда полотен изделия — полотно задать при выборе модели.

Изм.	Кол.уч	Лист	№ док.	Подп.	Дата
Разраб.		Кырлан А.С.			04.11.26
Пров.					
ГИП					
Н. контр.					
Утв.					

ГД-2026-012-АИ

Дом 120 м²

Общая площадь 147,36* м² · * размеры приняты, не замерены (реестр — л. 7–9, К-1)

Дизайн-проект интерьера

Стадия	Лист	Листов
РП	23	175

Ведомость заполнения проёмов

М б/м

Кырлан Александр Сергеевич


выпуск 04.11.2026 № 4dfa962484 · стр. 23 из 180

Лестница Л-1


План марша, разрез 1-1, узел крепления стойки ограждения, спецификация · отметки от ±0,000 (чистый пол этажа 1) · размеры в мм

ПРЕДВАРИТЕЛЬНО · не для производства работ · открыто пунктов: 11 (реестр — л. 7–9)

План марша Л-1* (М 1:50) · 2. Холл с лестницей

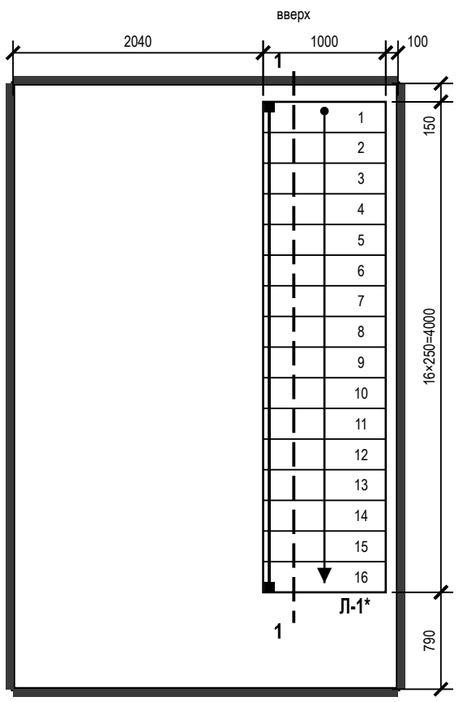


Разрез 1-1 (М 1:50)

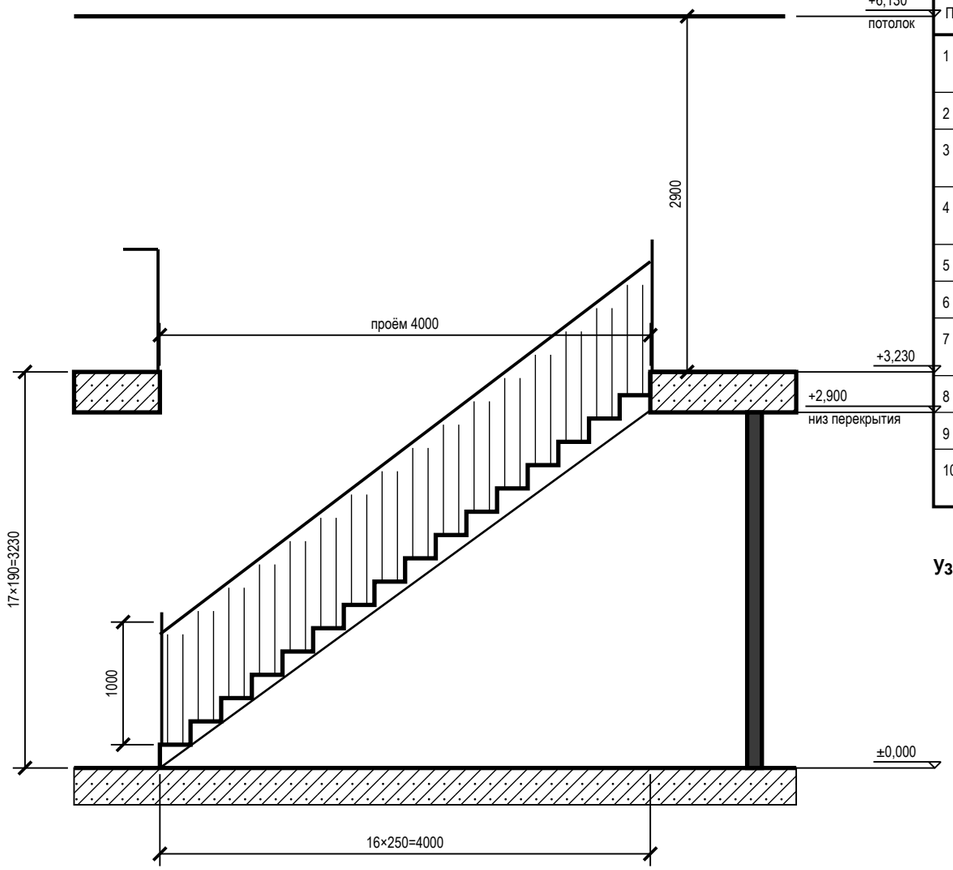

Спецификация элементов лестницы Л-1*

Поз.	Наименование	Кол.	Материал, сечение	Примечание
1	Ступень (проступь)	16	дуб табак, 40 мм	1000×250, толщина по изделию
2	Подступенок	17	дуб табак	высота 190
3	Косоур	2	косоуры стальные, тёплый графит	несущие марша
4	Столб ограждения марша	2	дуб табак, стойки — графит	по концам марша, стороны Г
5	Балясина	45	дуб табак, стойки — графит	шаг 110, просвет 80
6	Поручень марша	1	Ø40	L ≈ 5,02 м, h 900
7	Столб ограждения проёма	2	дуб табак, стойки — графит	углы проёма, стороны Г
8	Балясина ограждения проёма	36	дуб табак, стойки — графит	шаг 110
9	Поручень ограждения проёма	1	Ø40	L ≈ 4,00 м, h 1000
10	Крепёж ограждения	1	комплект по изделию	нагрузка на поручень 0,5 кН/м

Узел 1. Крепление стойки ограждения (М 1:5)

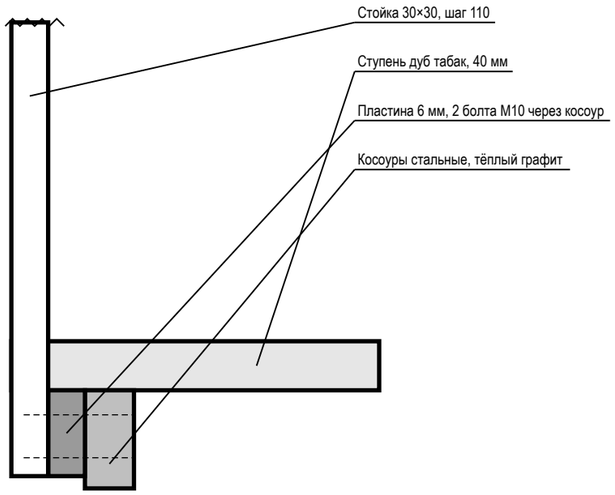

Зазор от низа заполнения до ступени — не более 100 (ГОСТ 25772-2025, прил. А, прим. 3)

Примечания

1. Лестница Л-1*: 17 подъёмов × 190 мм = 3230 мм (отм. ±0,000 … +3,230), проступь 250 мм, ширина марша 1000 мм; уклон 37,2°, шаг 2h + b = 630 мм (удобно 600–640 — практика).
2. Ограждение марша со стороны Г: балясины, просвет между элементами 80 мм (не больше 150 — ГОСТ 25772-2025, табл. 3, тип МВ); высота 1000 мм, поручень с одной стороны на 900 мм по линии носков (не менее 900 — СП 55.13330.2016, п. 8.3; СП 59.13330.2020, п. 6.2.11).
3. Проём в перекрытии 1000×4000 мм на этаже 2 ограждён со сторон Г высотой 1000 мм, непрерывно, с поручнем (СП 55.13330.2016, п. 8.3); нагрузка на поручень 0,5 кН/м (СП 20.13330.2016, п. 8.2.6).
4. Просвет над линией носков — не менее 2900 мм (ступень 17, под потолком мансарды); рекомендуется не менее 2000, путь эвакуации — 2200 (СП 55.13330.2016, п. 7.4).
5. Все подступенки одной высоты (СП 55.13330.2016, п. 8.2). Разность отметок чистых полов замерить до заказа изделия: высота подступенка — по замеру.
6. Узел 1 — типовое решение крепления стойки к косоуру; крепёж, сечения и материал — по проекту изделия изготовителя лестницы.

Допущения и предложения на листе

Основа листа: взаимное расположение помещений, контур дома 9600 × 8000 и раскладка этажей подобраны проектировщиком под габариты помещений брифа; обмер и проект АР — задание (К-1); высота потолка 2900 мм — по брифу, не замерена; перекрытие 330 мм и отметка 2-го этажа +3,230 приняты; проект КР — задание (К-2); наружные стены 400 мм, перегородки 120 мм приняты (в брифе толщин нет) (К-1); разрешённая мощность 15 кВт принята по типовым ТУ для частного дома (К-4); подрайон климата не задан — принят не северный (жилые от 2,5 м) (К-7).

Знак «*» — принято, не замерено и не подтверждено (замерить на объекте): К-3: Л-1 — место, тип и размеры лестницы брифом не заданы (только «лестница из холла 1-го этажа»): одномаршевая 17 × 190 × 250 вдоль стены Б холла — предложение проектировщика; конструкция и расчёт — проект КР.

См. лист открытых вопросов (лист 7, записи К-1–К-4; лист 8, запись К-7).

1000 мм · печать 1:1

Изм.	Кол.уч	Лист	№ док.	Подп.	Дата
Разраб.		Кырлан А.С.			04.11.26
Пров.					
ГИП					
Н. контр.					
Утв.					

ГД-2026-012-АИ

Дом 120 м²

Общая площадь 147,36* м² · * размеры приняты, не замерены (реестр — л. 7–9, К-1)

Дизайн-проект интерьера

Стадия	Лист	Листов
РП	24	175

Лестница Л-1

М 1:50

Кырлан Александр Сергеевич

выпуск 04.11.2026 · 4dfa962484 · стр. 24 из 180

Концепция интерьера · 1-й этаж


Средиземноморский · схема комплементарная · 60/30/10 · материалы, образы и зонирование

ПРЕДВАРИТЕЛЬНО · не для производства работ · открыто пунктов: 11 (реестр — л. 7–9)


Идея

Стиль — средиземноморский: солнце и воздух, морская свежесть, неторопливость, тёплая простота, жизнь на террасе. Средиземноморский 60 % + скандинавский 40 %: дом у соснового бора, светлый и солнечный. Стены — кремовый белый Calla G503, потолки — Loft White No. 222; второй план — светлый песок S 1010-Y20R, морская лазурь Lulworth Blue No. 89, серо-оливковая листва Treron No. 292; акценты — эгейский синий S 3050-R80B, охра India Yellow No. 66, олива S 5020-G90Y. По брифу: дерево — дуб табак (мебель, лестница), фурнитура и светильники — латунь, рамы и металл — тёплый графит; свет тёплый 2700–3000 K, фасады матовые. Цветовая схема — комплементарная, пропорция 60/30/10: база на стенах и потолках, вторичный цвет — в текстиле и мягкой мебели, акцент — точечно.


Мудборд: материалы и фактуры

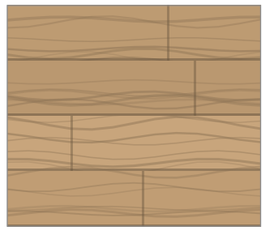

1167-4250
пол

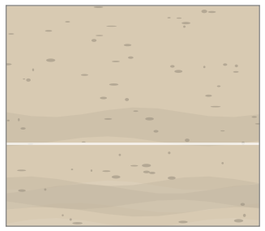

Керамогранит под травертин
фартук

 

Loft White · Little Greene No. 222
потолок




Calla · Tikkurila G503
стены, плинтус




Эгейский синий · NCS S 3050-R80B
акцент (стена А)



Олива · NCS S 5020-G90Y
акцент (стена А)

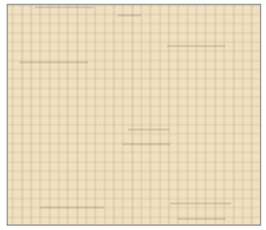

Лён, NCS S 1010-Y20R
портьеры-волна

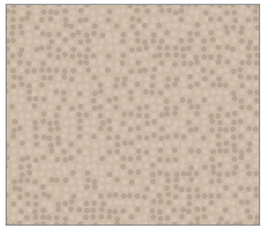

Шерсть, Tikkurila X463
ковёр в зоне отдыха, плед на диван



Бархат, NCS S 3050-R80B
подушки на диван

Палитра 60/30/10




60 % база — Tikkurila G503 Calla, LRV 89; Little Greene No. 222 Loft White, LRV 92

30 % вторичный — NCS S 1010-Y20R Светлый песок / известняк, LRV 75; Farrow & Ball No. 89 Lulworth Blue — светлая морская лазурь, LRV 45; Farrow & Ball No. 292 Treron — серо-оливковая листва, LRV 15

10 % акцент — NCS S 3050-R80B Эгейский синий, LRV 13; Farrow & Ball No. 66 India Yellow — охра / горчица итальянских фасадов, LRV 36; NCS S 5020-G90Y Олива, LRV 20

Функциональное зонирование (М 1:200)

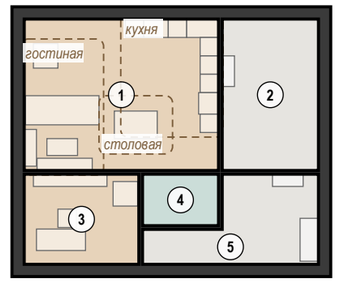

- дневная зона: гостиная, кухня, столовая
- мокрая зона: санузлы
- вход и коммуникации
- функциональная зона в помещении
- (1) номер помещения (лист 27)

Образы помещений

1. Гостиная-кухня — 31,32 м²

стены Tikkurila G503; акцент S 3050-R80B на стене А
пол — 1167-4250
текстиль: портьеры S 1010-Y20R, тюль No. 222, римская штора X463, ковёр в зоне отдыха X463
декор: картина над креслом, растение, ваза

3. Кабинет — 11,00 м²

стены Tikkurila G503; акцент S 5020-G90Y на стене А
пол — 1167-4250
текстиль: портьеры S 1010-Y20R, тюль No. 222, ковёр X463
декор: картина над креслом

5. Прихожая — 12,20 м²

стены Tikkurila G503
пол — A8UZ
декор: зеркало, Замиокулькас в кашпо
свет 3000/2700 K

2. Холл с лестницей — 15,51 м²

стены Tikkurila G503
пол — 1167-4250
декор: Сансевиерия в кашпо
свет 3000 K

4. Санузел гостевой — 4,17 м²

стены Atlas Concorde A8UZ
пол — керамогранит под травертин, матовый
декор: зеркало над умывальником
свет 3000 K

Материалы и отделка

1167-4250
пол — пом. 1, 2, 3

Керамогранит под травертин
матовый; 1200×600
фартук — пом. 1

Керамогранит ректифицированный под травертин
матовый; 600×600
пол — пом. 4

A8UZ
стены, пол — пом. 4, 5

Tikkurila G503 Calla, LRV 89
матовая
стены, плинтус — пом. 1, 2, 3, 5

Little Greene No. 222 Loft White, LRV 92
Little Greene Absolute Matt, глубокоматовая
потолок — пом. 1, 2, 3, 4, 5

NCS S 3050-R80B Эгейский синий, LRV 13
акцентная стена
акцент (стена А) — пом. 1

NCS S 5020-G90Y Олива, LRV 20
акцентная стена
акцент (стена А) — пом. 3

Текстиль и металл

Лён, NCS S 1010-Y20R
портьеры-волна

Вуаль, Little Greene No. 222
тюль

Лён, Tikkurila X463
римская штора

Шерсть, Tikkurila X463
ковёр в зоне отдыха, плед на диван

Букле, NCS S 1010-Y20R
подушки на диван, подушки декоративные на кровать

Бархат, NCS S 3050-R80B
подушки на диван

Бархат, NCS S 5020-G90Y
подушки на кровать

Шерсть, NCS S 5020-G90Y
плед на кровать

Чёрный матовый металл
зеркало

Чего избегаем

1) Глянец и пластик под камень
2) Холодный белый 6500 K и LED-ленты холодного оттенка
3) Ракушки, якоря, штурвалы толпой — это морской китч, не средиземноморье
4) Ярко-синие стены в северной комнате без тёплой основы
5) Глянцевая кафельная плитка под котто
6) Тяжёлые портьеры и ламбрекены

Примечания

1. Коды цвета — по веерам производителей (колерная карта, лист 83); перед закупкой краски — выкрас на стене объекта под дневным светом и лампами проекта.
2. Материалы — по ведомости отделки (лист 80); мебель, текстиль и декор — по спецификации (лист 29). Образцы доски, керамогранита и тканей утвердить до заказа.
3. Фактуры на листе условные, цвет передан по HEX-значениям производителей: при печати возможны отклонения, решение — только по физическому образцу.

Допущения и предложения на листе

Основа листа: взаимное расположение помещений, контур дома 9600 × 8000 и раскладка этажей подобраны проектировщиком под габариты помещений брифа; обмер и проект АР — задание (К-1); высота потолка 2900 мм — по брифу, не замерена; перекрытие 330 мм и отметка 2-го этажа +3,230 приняты; проект КР — задание (К-2); наружные стены 400 мм, перегородки 120 мм приняты (в брифе толщин нет) (К-1); разрешённая мощность 15 кВт принята по типовым ТУ для частного дома (К-4); подрайон климата не задан — принят не северный (жилые от 2,5 м) (К-7).
См. лист открытых вопросов (лист 7, записи К-1, К-2, К-4; лист 8, запись К-7).

Изм.	Кол.уч	Лист	№ док.	Подп.	Дата
Разраб.		Кырлан А.С.			04.11.26
Пров.					
ГИП					
Н. контр.					
Утв.					

ГД-2026-012-АИ

Дом 120 м²

Общая площадь 147,36* м² · * размеры приняты, не замерены (реестр — л. 7–9, К-1)

Дизайн-проект интерьера	Стадия	Лист	Листов
	РП	25	175

Концепция интерьера · 1-й этаж

М б/м

Кырлан Александр Сергеевич

выпуск 04.11.2026 № 4dfa962484 · стр. 25 из 180

Концепция интерьера · 2-й этаж


Средиземноморский · схема комплементарная · 60/30/10 · материалы, образы и зонирование

ПРЕДВАРИТЕЛЬНО · не для производства работ · открыто пунктов: 11 (реестр — л. 7–9)


Идея

Стиль — средиземноморский: солнце и воздух, морская свежесть, неторопливость, тёплая простота, жизнь на террасе. Средиземноморский 60 % + скандинавский 40 %: дом у соснового бора, светлый и солнечный. Стены — кремовый белый Calla G503, потолки — Loft White No. 222; второй план — светлый песок S 1010-Y20R, морская лазурь Lulworth Blue No. 89, серо-оливковая листва Treron No. 292; акценты — эгейский синий S 3050-R80B, охра India Yellow No. 66, олива S 5020-G90Y. По брифу: дерево — дуб табак (мебель, лестница), фурнитура и светильники — латунь, рамы и металл — тёплый графит; свет тёплый 2700–3000 K, фасады матовые. Цветовая схема — комплементарная, пропорция 60/30/10: база на стенах и потолках, вторичный цвет — в текстиле и мягкой мебели, акцент — точечно.

Мудборд: материалы и фактуры

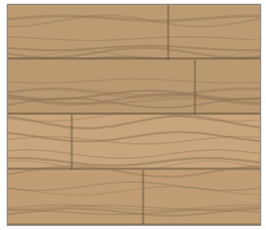

1167-4250
пол

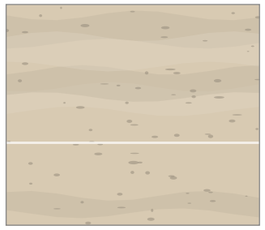

Керамогранит ректифицированный под травертин
пол



Loft White · Little Greene No. 222
потолок, стены, плинтус



Calla · Tikkurila G503
стены, плинтус



NCS S 0502-Y
стены



NCS S 0300-N
потолок, плинтус



Lulworth Blue — светлая морская лазурь · Farrow & Ball No. 89
акцент (стена А)



India Yellow — охра / горчица итальянских фасадов · Farrow & Ball No. 66
акцент (стена А)



Tikkurila H440
акцент (стена А)

Палитра 60/30/10



60 % база — Tikkurila G503 Calla, LRV 89; Little Greene No. 222 Loft White, LRV 92

30 % вторичный — NCS S 1010-Y20R Светлый песок / известняк, LRV 75; Farrow & Ball No. 89 Lulworth Blue — светлая морская лазурь, LRV 45; Farrow & Ball No. 292 Treron — серо-оливковая листва, LRV 15

10 % акцент — NCS S 3050-R80B Эгейский синий, LRV 13; Farrow & Ball No. 66 India Yellow — охра / горчица итальянских фасадов, LRV 36; NCS S 5020-G90Y Олива, LRV 20

Функциональное зонирование (М 1:200)



- ночная зона: спальни
- мокрая зона: санузлы
- хранение: гардеробная, кладовая
- вход и коммуникации
- (1) номер помещения (лист 27)

Образы помещений

6. Спальня родителей — 17,17 м²

стены Tikkurila G503; акцент No. 89 на стене А
пол — 1167-4250
текстиль: портьеры S 1010-Y20R, тюль No. 222, ковёр X395
декор: картина над кроватью, Аглаонема в кашпо
свет 2700 K, сценарии: вечер, уборка

7. Детская — 12,30 м²

стены Tikkurila G503; акцент No. 66 на стене А
пол — 1167-4250
текстиль: портьеры S 1010-Y20R, тюль No. 222, ковёр X463
декор: картина над кроватью, зеркало в рост
свет 2700 K, сценарии: вечер

12. Детская вторая — 9,23 м²

стены Tikkurila G503; акцент H440 на стене А
пол — 1167-4250
текстиль: портьеры S 1010-Y20R, тюль No. 222, ковёр X463
декор: картина над кроватью, зеркало в рост
свет 2700 K, сценарии: вечер

10. Холл второго этажа — 15,51 м²

стены Tikkurila G503
пол — 1167-4250
декор: Хлорофитум в кашпо
свет 3000 K

11. Коридор второго этажа — 5,16 м²

стены Tikkurila G503
пол — 1167-4250
декор: Сансевиерия в кашпо
свет 3000 K

8. Гардеробная — 3,82 м²

стены Little Greene No. 222
пол — 1167-4250
свет 3000 K

13. Санузел второго этажа — 5,31 м²

стены Atlas Concorde A8UZ
пол — керамогранит под травертин, матовый
декор: зеркало над умывальником
свет 3000 K

9. Кладовая — 4,66 м²

стены NCS S 0502-Y
пол — 1167-4250
свет 3000 K

Материалы и отделка

1167-4250
пол — пом. 6, 7, 8, 9, 10, 11, 12

Керамогранит ректифицированный под травертин
матовый; 600×600
пол — пом. 13

A8UZ
стены — пом. 13

Tikkurila G503 Calla, LRV 89
матовая
стены, плинтус — пом. 6, 7, 10, 11, 12

Little Greene No. 222 Loft White, LRV 92
Little Greene Absolute Matt, глубокоматовая
потолок, стены, плинтус — пом. 6, 7, 8, 10, 11, 12, 13

NCS S 0502-Y, LRV 86
матовая
стены — пом. 9

NCS S 0300-N, LRV 92
глубокоматовая
потолок, плинтус — пом. 9

Farrow & Ball No. 89 Lulworth Blue — светлая морская лазурь, LRV 45
акцентная стена
акцент (стена А) — пом. 6

Farrow & Ball No. 66 India Yellow — охра / горчица итальянских фасадов, LRV 36
акцентная стена
акцент (стена А) — пом. 7

Текстиль и металл

Лён, NCS S 1010-Y20R
портьеры-волна, подушки декоративные на кровать

Шерсть, Tikkurila X395
ковёр под кроватью

Шерсть, Farrow & Ball No. 89
плед на кровать

Букле, NCS S 1010-Y20R
подушки декоративные на кровать

Шерсть, Farrow & Ball No. 66
плед на кровать

Вуаль, Little Greene No. 222
тюль

Бархат, Farrow & Ball No. 89
подушки на кровать

Шерсть, Tikkurila X463
ковёр под кроватью

Бархат, Farrow & Ball No. 66
подушки на кровать

Чёрный матовый металл
зеркало в рост

Чего избегаем

1) Глянец и пластик под камень
2) Холодный белый 6500 K и LED-ленты холодного оттенка
3) Ракушки, якоря, штурвалы толпой — это морской китч, не средиземноморье
4) Ярко-синие стены в северной комнате без тёплой основы
5) Глянцевая кафельная плитка под котто
6) Тяжёлые портьеры и ламбрекены

Допущения и предложения на листе. Основа листа: взаимное расположение помещений, контур дома 9600 × 8000 и раскладка этажей подобраны проектировщиком под габариты помещений брифа; обмер и проект АР — задание (К-1); высота потолка 2900 мм — по брифу, не замерена; перекрытие 330 мм и отметка 2-го этажа +3,230 приняты; проект КР — задание (К-2); наружные стены 400 мм, перегородки 120 мм приняты (в брифе толщин нет) (К-1); разрешённая мощность 15 кВт принята по типовым ТУ для частного дома (К-4); подрайон климата не задан — принят не северный (жилые от 2,5 м) (К-7). Знак «*» — принято, не замерено и не подтверждено (замерить на объекте): К-2: отметка чистого пола этажа «2-й этаж» +3,230 — отметка чистого пола 2-го этажа +3,230 принята: высота потолка 2900 по брифу + перекрытие с полом 330 (конструкция перекрытия не задана; проект КР — задание). См. лист открытых вопросов (лист 7, записи К-1, К-2, К-4; лист 8, запись К-7).

Примечания

1. Коды цвета — по веерам производителей (колерная карта, лист 83); перед закупкой краски — выкрас на стене объекта под дневным светом и лампами проекта.
2. Материалы — по ведомости отделки (лист 80); мебель, текстиль и декор — по спецификации (лист 29). Образцы доски, керамогранита и тканей утвердить до заказа.
3. Фактуры на листе условные, цвет передан по HEX-значениям производителей: при печати возможны отклонения, решение — только по физическому образцу.

Изм.	Кол.уч	Лист	№ док.	Подп.	Дата
Разраб.		Кырлан А.С.			04.11.26
Пров.					
ГИП					
Н. контр.					
Утв.					

ГД-2026-012-АИ

Дом 120 м²

Общая площадь 147,36* м² · * размеры приняты, не замерены (реестр — л. 7–9, К-1)

Дизайн-проект интерьера

Стадия	Лист	Листов
РП	26	175

Концепция интерьера · 2-й этаж


М б/м

Кырлан Александр Сергеевич

выпуск 04.11.2026 № 4dfa962484 · стр. 26 из 180

План расстановки мебели · 1-й этаж

Мебель и оборудование · размеры в мм от чистовых стен · марки — по ведомости

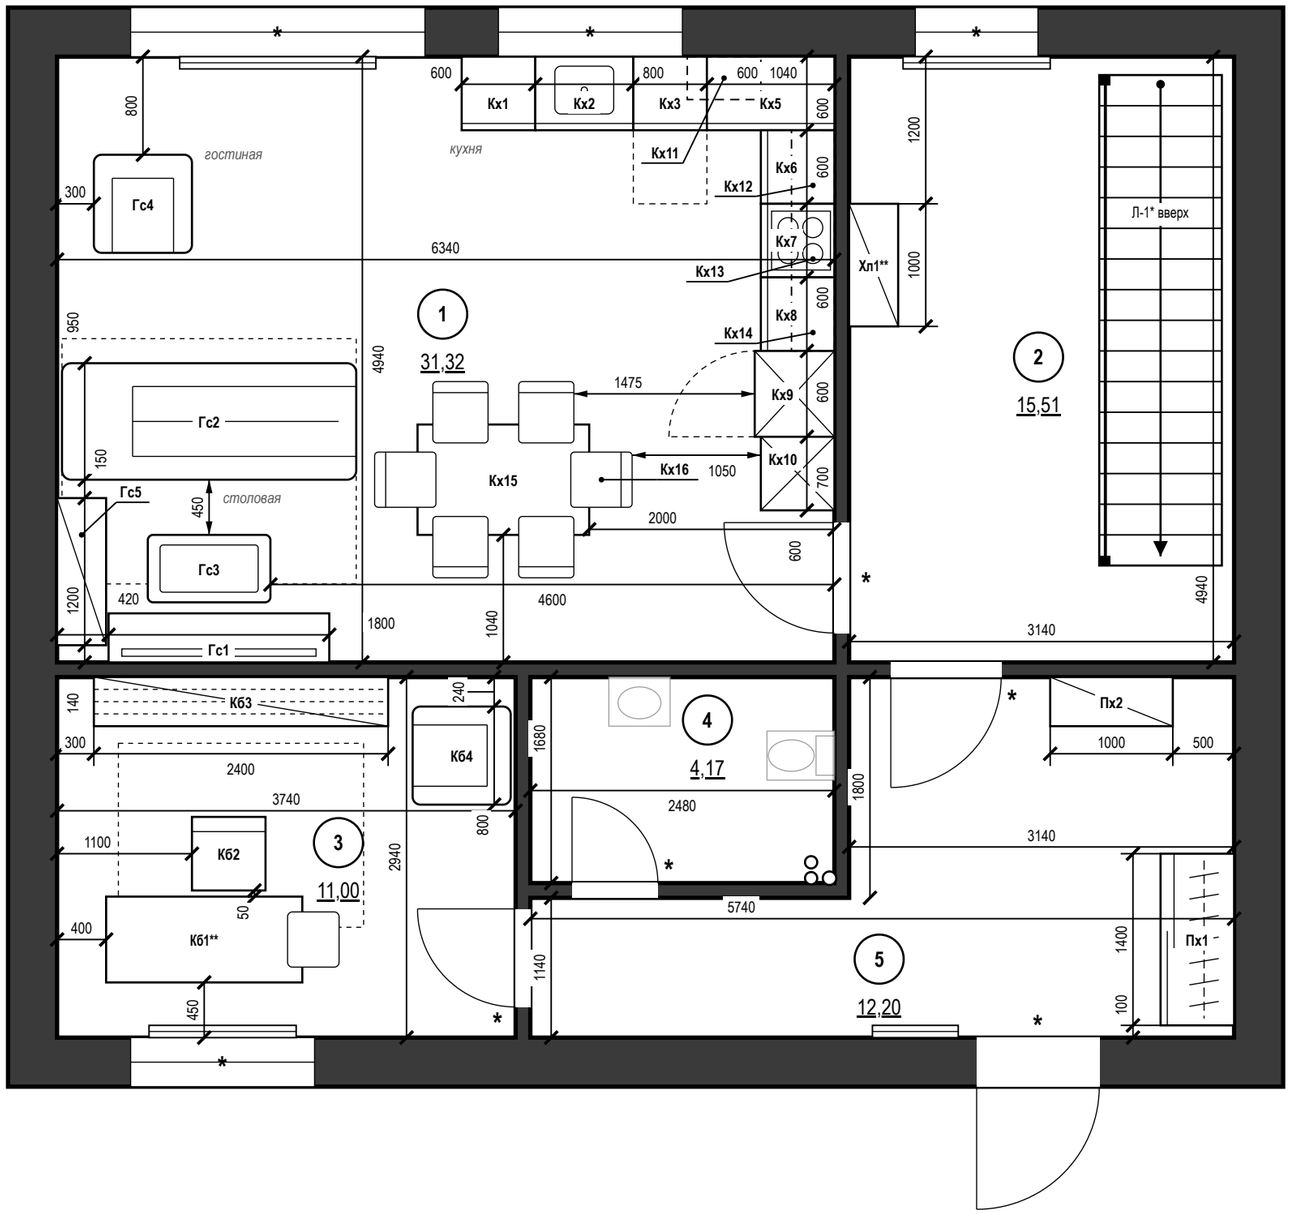

1000 мм · печать 1:1

Экспликация помещений

лист 17 · на плане — номера в марках

Ведомость мебели и оборудования

27 позиц. (32 шт.) — не помещается на листе:
полностью на листе 29 «Спецификация мебели и оборудования»
марка, наименование, Ш×Г×В, материал, модель,
допуск замены. Марки на плане — по ней.

Условные обозначения

- мебель и оборудование — габарит в масштабе
- навесные шкафы (низ выше 0,9 м) — невидимый контур
- ковёр
- зона открывания дверец шкафов и техники
- К1 — марка предмета по ведомости мебели
- привязка от чистовой стены, мм
- ширина прохода, зазор, мм
- сантехприборы — подложка (лист ВК)
- радиатор отопления (лист ОВ)
- существующие стены (сечение)
- * — «*» — принято, не замерено и не подтверждено
- стояк: К1 — канализация, В1 — ХВС, Т3 — ГВС
- 1 — номер помещения, площадь м²
- *зона* — функциональная зона помещения

Допущения и предложения на листе

Основа листа: взаимное расположение помещений, контур дома 9600 × 8000 и раскладка этажей подобраны проектировщиком под габариты помещений брифа; обмер и проект АР — задание (К-1); высота потолка 2900 мм — по брифу, не замерена; перекрытие 330 мм и отметка 2-го этажа +3,230 приняты; проект КР — задание (К-2); наружные стены 400 мм, перегородки 120 мм приняты (в брифе толщин нет) (К-1); разрешённая мощность 15 кВт принята по типовым ТУ для частного дома (К-4); подрайон климата не задан — принят не северный (жилые от 2,5 м) (К-7).
Знак «*» — принято, не замерено и не подтверждено (замерить на объекте): К-1: окно пом. 1 (стена А), 2 (А), 3 (В) — окно: место, ширина, высота и подоконник приняты по брифу, стена — по раскладке проектировщика (К-1), не замерены; дверь пом. 1 (стена Б), 3 (Б), 4 (В), 5 (А) — проём: место и ширина приняты проектировщиком по брифу (раскладка этажей — К-1), не замерены; дверь пом. 5 (стена В) — входная дверь: место и ширина проёма приняты проектировщиком по брифу (без плана дома), не замерены; К-3: Л-1 — место, тип и размеры лестницы брифом не заданы (только «лестница из холла 1-го этажа»): одномаршевая 17 × 190 × 250 вдоль стены Б холла — предложение проектировщика; конструкция и расчёт — проект КР; К-5: Ст К1-1, Ст В1-1, Ст Т3-1, Ст К1-2 (кухня), Ст В1-2, Ст Т3-2 — положение стояка принято проектировщиком (проект ВК дома не передан), не замерено.
Знак «**» — предложение проектировщика, заказчиком не утверждено (согласовать с заказчиком): ИЗ-2: Хл1 — Было под окном стены А (700…1700) на радиаторе Рд3 (500…1700): прибор в корпусе; Кб1 — Было у стены В offset 400…2000 вплотную над радиатором Рд4 (750…1950): прибор в корпусе.
Открытые вопросы и конфликты по листу: К-1.
Изменения по листу без подписи: ИЗ-1, ИЗ-2.
См. лист открытых вопросов (лист 7, записи К-1–К-5; лист 8, запись К-7; лист 9, записи ИЗ-1, ИЗ-2).

Примечания

1. Размеры — в мм от чистовых поверхностей стен, размеры помещений — в свету, привязки — от стен, углов помещения и соседних предметов, проходы и зазоры — стрелками; розетки и выводы под мебель — лист 34, выключатели — лист 38, сантехприборы лист 52.
2. Общие указания к расстановке (чистовой слой, контрольный обмер, зазоры встроенной мебели, замена покупной) — примечания к спецификации, лист 29.
3. Отступ от стены, на плане не образмерен: Гс2 — 40 мм, Кб4 — 40 мм.
4. Стулья обеденной группы (Кх16 — 6 шт.) показаны в рабочем положении, задвинутыми под столешницу на 150 мм.

Изм.	Кол.уч	Лист	№ док.	Подп.	Дата
Разраб.		Кырлан А.С.			04.11.26
Пров.					
ГИП					
Н. контр.					
Утв.					

ГД-2026-012-АИ

Дом 120 м²

Общая площадь 147,36* м² · * размеры приняты, не замерены (реестр — л. 7–9, К-1)

Дизайн-проект интерьера	Стадия	Лист	Листов
	РП	27	175

План расстановки мебели · 1-й этаж


М 1:50

Кырлан Александр Сергеевич

выпуск 04.11.2026 № 4dfa962484 · стр. 27 из 180

План расстановки мебели · 2-й этаж

Мебель и оборудование · размеры в мм от чистовых стен · марки — по ведомости

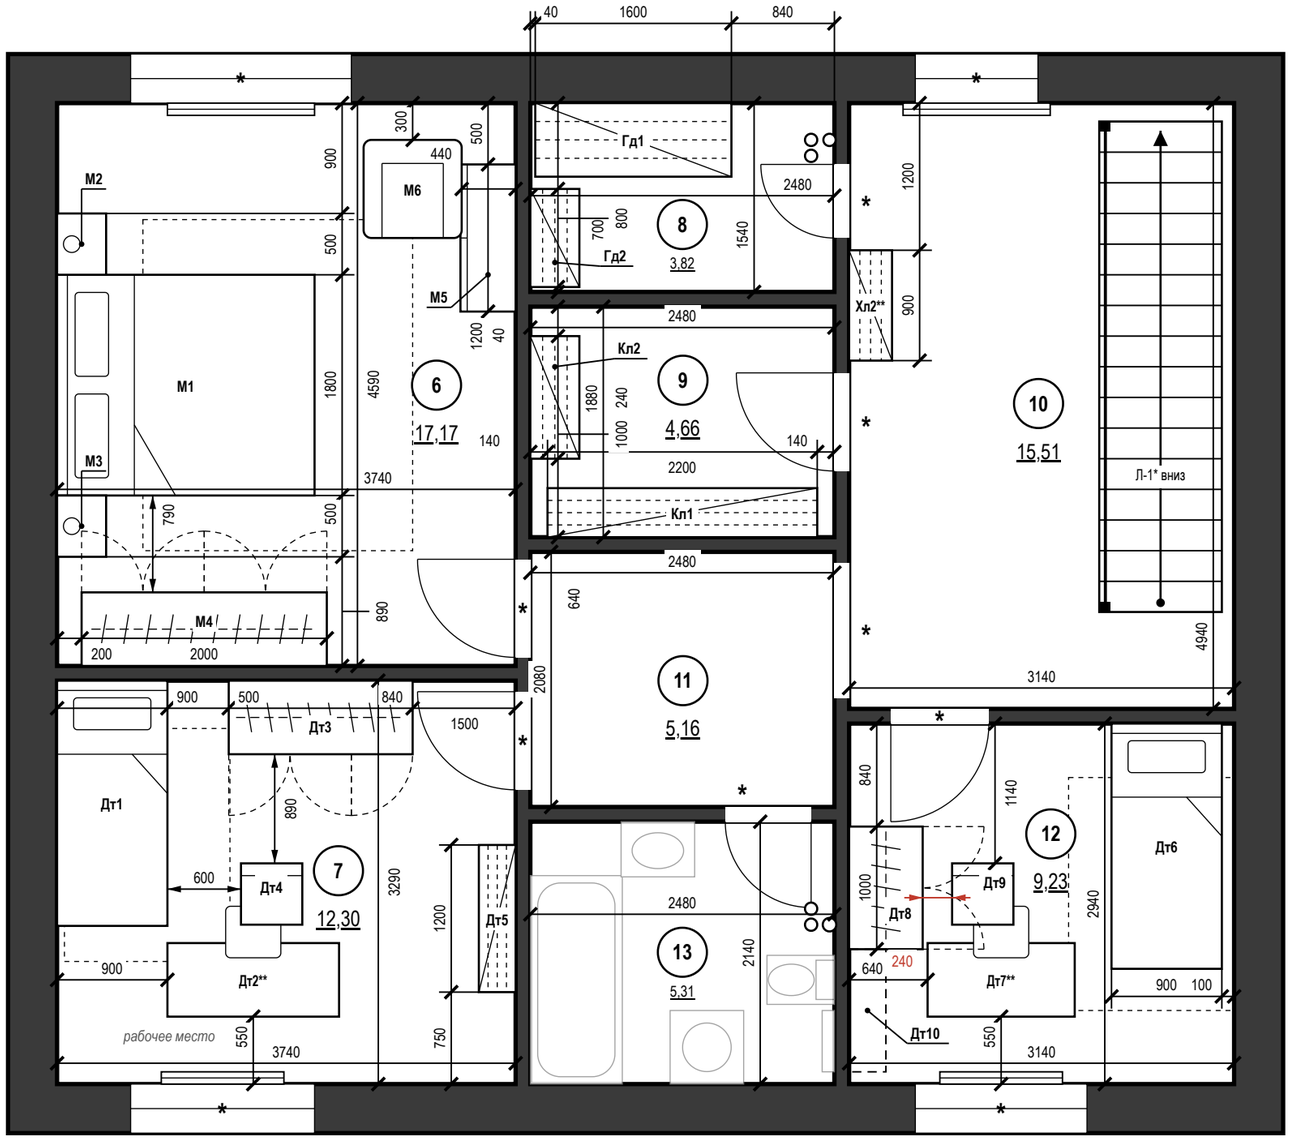

Экспликация помещений

лист 18 · на плане — номера в марках

Ведомость мебели и оборудования

21 позиц. (21 шт.) — не помещается на листе:
полностью на листе 29 «Спецификация мебели и оборудования»
марка, наименование, Ш×Г×В, материал, модель,
допуск замены. Марки на плане — по ней.

Условные обозначения

- мебель и оборудование — габарит в масштабе
- навесные шкафы (низ выше 0,9 м) — невидимый контур
- ковёр
- зона открывания дверец шкафов и техники
- К1 — марка предмета по ведомости мебели
- привязка от чистовой стены, мм
- ширина прохода, зазор, мм
- проход меньше нормы — расстановку изменить
- сантехприборы — подложка (лист ВК)
- радиатор отопления (лист ОВ)
- существующие стены (сечение)
- * — «*» — принято, не замерено и не подтверждено
- стояк: К1 — канализация, В1 — ХВС, Т3 — ГВС
- 1 — номер помещения, площадь м²
- *зона* — функциональная зона помещения

Допущения и предложения на листе

Основа листа: взаимное расположение помещений, контур дома 9600 × 8000 и раскладка этажей подобраны проектировщиком под габариты помещений брифа; обмер и проект АР — задание (К-1); высота потолка 2900 мм — по брифу, не замерена; перекрытие 330 мм и отметка 2-го этажа +3,230 приняты; проект КР — задание (К-2); наружные стены 400 мм, перегородки 120 мм приняты (в брифе толщин нет) (К-1); разрешённая мощность 15 кВт принята по типовым ТУ для частного дома (К-4); подрайон климата не задан — принят не северный (жилые от 2,5 м) (К-7).

Знак «*» — принято, не замерено и не подтверждено (замерить на объекте): К-1: окно пом. 6 (стена А), 7 (В), 10 (А), 12 (В) — окно: место, ширина, высота и подоконник приняты по брифу, стена — по раскладке проектировщика (К-1), не замерены; дверь пом. 6 (стена Б), 7 (Б), 8 (Б), 9 (Б), 11 (Б), 12 (А) — проём: место и ширина приняты проектировщиком по брифу (раскладка этажей — К-1), не замерены; дверь пом. 13 (стена А) — Петли у правого откоса (х 6150, у стояков): открытое полотно стоит вдоль стены Б, вошедший идёт влево к умывальнику и ванне;

К-2: отметка чистого пола этажа «2-й этаж» +3,230 — отметка чистого пола 2-го этажа +3,230 принята: высота потолка 2900 по брифу + перекрытие с полом 330 (конструкция перекрытия не задана; проект КР — задание);

К-3: Л-1 — место, тип и размеры лестницы брифом не заданы (только «лестница из холла 1-го этажа»): одномаршевая 17 × 190 × 250 вдоль стены Б холла — предложение проектировщика; конструкция и расчёт — проект КР; К-5: Ст К1-1, Ст В1-1, Ст Т3-1, Ст К1-2 (кухня), Ст В1-2, Ст Т3-2 — положение стояка принято проектировщиком (проект ВК дома не передан), не замерено.

Знак «**» — предложение проектировщика, заказчиком не утверждено (согласовать с заказчиком): ИЗ-2: Дт2 — Было у стены В offset 900…2300 над радиатором Рд6 (850…1850); Хл2 — Было под окном стены А (700…1600) перед радиатором Рд7 (500…1700); Дт7 — Было у стены В offset 600…1800 над радиатором Рд8 (800…1800).

Открытые вопросы и конфликты по листу: К-1.

Изменения по листу без подписи: ИЗ-1, ИЗ-2.

См. лист открытых вопросов (лист 7, записи К-1–К-5; лист 8, запись К-7; лист 9, записи ИЗ-1, ИЗ-2).

Примечания

1. Размеры — в мм от чистовых поверхностей стен, размеры помещений — в свету, привязки — от стен, углов помещения и соседних предметов, проходы и зазоры — стрелками; розетки и выводы под мебель — лист 35, выключатели — лист 39, сантехприборы лист 53.
2. Общие указания к расстановке (чистовой слой, контрольный обмер, зазоры встроенной мебели, замена покупной) — примечания к спецификации, лист 29.

1000 мм · печать 1:1

Изм.	Кол.уч	Лист	№ док.	Подп.	Дата
Разраб.		Кырлан А.С.			04.11.26
Пров.					
ГИП					
Н. контр.					
Утв.					

ГД-2026-012-АИ

Дом 120 м²

Общая площадь 147,36* м² · * размеры приняты, не замерены (реестр — л. 7–9, К-1)

Дизайн-проект интерьера

Стадия	Лист	Листов
РП	28	175

План расстановки мебели · 2-й этаж

М 1:50

Кырлан Александр Сергеевич

выпуск 04.11.2026 № 4dfa962484 · стр. 28 из 180

01

Планировочное решение

Кырлан Александр Сергеевич

Спецификация мебели и оборудования

ПРЕДВАРИТЕЛЬНО · не для производства работ · открыто пунктов: 11 (реестр — л. 7–9)

Форма 1 ГОСТ 21.110-2013 · позиции мебели — по плану расстановки

Поз.	Наименование и техническая характеристика	Тип, марка, обозначение документа, опросного листа	Код продукции	Поставщик	Ед. измерения	Кол.	Масса 1 ед., кг	Примечание
	Мебель встроенная и корпусная (изготовление по чертежам мебельщика)							
Кх1	Модуль с ящиками; корпус ЛДСП 16 мм; фасады — МДФ 18 мм, эмаль матовая; цвет фасадов — в цвет стен (Tikkurila G503); Ш×Г×В 600×600×900 мм			изготовление на заказ	шт.	1		пом. 1
Кх2	Модуль под мойку у окна; корпус ЛДСП 16 мм; фасады — МДФ 18 мм, эмаль матовая; цвет фасадов — в цвет стен (Tikkurila G503); Ш×Г×В 800×600×900 мм			изготовление на заказ	шт.	1		пом. 1
Кх3	Модуль под встраиваемую ПММ 60; без корпуса (ниша между соседними модулями); фасад на дверь машины — МДФ 18 мм, эмаль матовая; цоколь; цвет фасадов — в цвет стен (Tikkurila G503); Ш×Г×В 600×600×900 мм			изготовление на заказ	шт.	1		пом. 1
Кх5	Модуль угловой глухой, поворотные полки; корпус ЛДСП 16 мм; фасады — МДФ 18 мм, эмаль матовая; цвет фасадов — в цвет стен (Tikkurila G503); Ш×Г×В 1040×600×900 мм			изготовление на заказ	шт.	1		пом. 1
Кх6	Модуль с ящиками; корпус ЛДСП 16 мм; фасады — МДФ 18 мм, эмаль матовая; цвет фасадов — в цвет стен (Tikkurila G503); Ш×Г×В 600×600×900 мм			изготовление на заказ	шт.	1		пом. 1
Кх7	Модуль с варочной панелью и духовым шкафом; корпус ЛДСП 16 мм; фасады — МДФ 18 мм, эмаль матовая; цвет фасадов в цвет стен (Tikkurila G503); Ш×Г×В 600×600×900 мм			изготовление на заказ	шт.	1		пом. 1
Кх8	Модуль с ящиками; корпус ЛДСП 16 мм; фасады — МДФ 18 мм, эмаль матовая; цвет фасадов — в цвет стен (Tikkurila G503); Ш×Г×В 600×600×900 мм			изготовление на заказ	шт.	1		пом. 1
Кх9	Колонна с холодильником; корпус ЛДСП 16 мм; фасады — МДФ 18 мм, эмаль матовая; цвет фасадов — в цвет стен (Tikkurila G503); Ш×Г×В 700×650×2200 мм			изготовление на заказ	шт.	1		пом. 1
Кх10	Пенал-кладовая с выдвижными корзинами; корпус ЛДСП 16 мм; фасады — МДФ 18 мм, эмаль матовая; цвет фасадов — в цвет стен (Tikkurila G503); Ш×Г×В 600×600×2200 мм			изготовление на заказ	шт.	1		пом. 1
Кх11	Навесной шкаф у окна, витрина со стеклом; корпус ЛДСП 16 мм; фасады — МДФ 18 мм, эмаль матовая; цвет фасадов — в цвет стен (Tikkurila G503); Ш×Г×В 600×350×900 мм			изготовление на заказ	шт.	1		пом. 1
Кх12	Навесной шкаф, фасад в тон цоколя; корпус ЛДСП 16 мм; фасады — МДФ 18 мм, эмаль матовая; цвет фасадов — в цвет стен (Tikkurila G503); Ш×Г×В 600×350×900 мм			изготовление на заказ	шт.	1		пом. 1
Кх13	Вытяжка встраиваемая в навесной шкаф; корпус ЛДСП 16 мм; фасады — МДФ 18 мм, эмаль матовая; цвет фасадов — в цвет стен (Tikkurila G503); Ш×Г×В 600×350×800 мм			изготовление на заказ	шт.	1		пом. 1
Кх14	Навесной шкаф с сушкой для посуды; корпус ЛДСП 16 мм; фасады — МДФ 18 мм, эмаль матовая; цвет фасадов — в цвет стен (Tikkurila G503); Ш×Г×В 600×350×900 мм			изготовление на заказ	шт.	1		пом. 1
Пх1	Шкаф-купе до потолка, дуб табак, планка-компенсатор до подшивки; корпус ЛДСП 16 мм; фасады — ЛДСП 10 мм в алюминиевом профиле; Ш×Г×В 1400×600×2650 мм			изготовление на заказ	шт.	1		пом. 5
М4	Шкаф распашной до потолка, фасады матовые; корпус ЛДСП 16 мм; фасады — МДФ 18 мм, эмаль матовая; цвет фасадов в цвет стен (Tikkurila G503); Ш×Г×В 2000×600×2600 мм			изготовление на заказ	шт.	1		пом. 6
Дт3	Шкаф распашной; корпус ЛДСП 16 мм; фасады — МДФ 18 мм, эмаль матовая; цвет фасадов — в цвет стен (Tikkurila G503); Ш×Г×В 1500×600×2200 мм			изготовление на заказ	шт.	1		пом. 7
Гд1	Система хранения: штанги, полки, ящики; каркас и полки — ЛДСП 16 мм, декор «дуб натуральный»; без фасадов; Ш×Г×В 1600×600×2600 мм			изготовление на заказ	шт.	1		пом. 8; крепление к стене

Примечания

1. Позиции мебели совпадают с марками на плане расстановки (лист 27); размеры Ш×Г×В — Ш вдоль стены, Г от стены.
2. Размеры и привязки плана расстановки — в мм от чистовых поверхностей стен: слой штукатурки 20 мм по блоку и 5 мм шпаклёвки по ГКЛ учтён; привязки — от стен и углов помещения, а не от другой мебели.
3. План расстановки не является документацией для изготовления мебели. Встроенная и корпусная мебель изготавливается по чертежам мебельщика после контрольного обмера (после штукатурки); «стена в стену» — с зазором 10 мм с каждой стороны или с компенсаторами; графы «Тип, марка» и «Код продукции» для неё не заполняются (ГОСТ 21.110-2013).
4. Покупные изделия — аналог по характеристикам: заменять только на изделия не больше указанного габарита и того же материала и цвета.
5. Материал и цвет, не указанные в данных изделия, приняты по концепции (лист 25): тон дерева — по полу, обивка — по вторичному цвету палитры; образцы согласовать до заказа.
6. Масса 1 ед. для изделий до 25 кг не указывается. Техника — по монтажным схемам изготовителя; выводы — по листам ЭОМ и ВК.

Допущения и предложения на листе

Основа листа: взаимное расположение помещений, контур дома 9600 × 8000 и раскладка этажей подобраны проектировщиком под габариты помещений брифа; обмер и проект АР — задание (К-1); высота потолка 2900 мм — по брифу, не замерена; перекрытие 330 мм и отметка 2-го этажа +3,230 приняты; проект КР — задание (К-2); наружные стены 400 мм, перегородки 120 мм приняты (в брифе толщин нет) (К-1); разрешённая мощность 15 кВт принята по типовым ТУ для частного дома (К-4); подрайон климата не задан — принят не северный (жилые от 2,5 м) (К-7).

См. лист открытых вопросов (лист 7, записи К-1, К-2, К-4; лист 8, запись К-7).

Изм.	Кол.уч	Лист	№ док.	Подп.	Дата
Разраб.		Кырлан А.С.			04.11.26
Пров.					
ГИП					
Н. контр.					
Утв.					

ГД-2026-012-АИ

Дом 120 м²

Общая площадь 147,36* м² · * размеры приняты, не замерены (реестр — л. 7–9, К-1)

Дизайн-проект интерьера

Стадия	Лист	Листов
РП	29	175

Спецификация мебели и оборудования

М б/м

Кырлан Александр Сергеевич

выпуск 04.11.2026 № 4dfa962484 · стр. 30 из 180

Спецификация мебели и оборудования (продолжение)

Форма 1 ГОСТ 21.110-2013 · позиции мебели — по плану расстановки

ПРЕДВАРИТЕЛЬНО · не для производства работ · открыто пунктов: 11 (реестр — л. 7–9)

Поз.	Наименование и техническая характеристика	Тип, марка, обозначение документа, опросного листа	Код продукции	Поставщик	Ед. измерения	Кол.	Масса 1 ед., кг	Примечание
Гд2	Полки для обуви и сумок; каркас и полки — ЛДСП 16 мм, декор «дуб натуральный»; без фасадов; Ш×Г×В 800×400×2000 мм			изготовление на заказ	шт.	1		пом. 8; крепление к стене
Кл1	Стеллаж для хранения; каркас и полки — ЛДСП 16 мм, декор «дуб натуральный»; без фасадов; Ш×Г×В 2200×400×2200 мм			изготовление на заказ	шт.	1		пом. 9; крепление к стене
Кл2	Стеллаж узкий для бытовой техники; каркас и полки — ЛДСП 16 мм, декор «дуб натуральный»; без фасадов; Ш×Г×В 1000×400×2200 мм			изготовление на заказ	шт.	1		пом. 9; крепление к стене
Дт8	Шкаф распашной; корпус ЛДСП 16 мм; фасады — МДФ 18 мм, эмаль матовая; цвет фасадов — в цвет стен (Tikkurila G503); Ш×Г×В 1000×600×2200 мм			изготовление на заказ	шт.	1		пом. 12
Дт10	Полки открытые над столом; каркас и полки — ЛДСП 16 мм, декор «дуб натуральный»; без фасадов; Ш×Г×В 1000×300×1200 мм			изготовление на заказ	шт.	1		пом. 12; крепление к стене
	Мебель покупная							
Гс1	ТВ-тумба подвесная с экраном, дуб табак; шпон, дуб натуральный, матовое масло; Ш×Г×В 1800×400×600 мм			аналог по характеристикам	шт.	1		пом. 1; замена ≤ габарита
Гс2	Диван трёхместный, лён; обивка — ткань, цвет NCS S 1010-Y20R; Ш×Г×В 950×2400×820 мм			аналог по характеристикам	шт.	1		пом. 1; замена ≤ габарита
Гс3	Столик журнальный, дуб и латунь; шпон, дуб натуральный, матовое масло; Ш×Г×В 1000×550×420 мм			аналог по характеристикам	шт.	1		пом. 1; замена ≤ габарита
Гс4	Кресло у окна, букле; обивка — ткань, цвет NCS S 1010-Y20R; Ш×Г×В 800×800×850 мм			аналог по характеристикам	шт.	1		пом. 1; замена ≤ габарита
Гс5	Буфет низкий, дуб табак; шпон, дуб натуральный, матовое масло; Ш×Г×В 1200×400×800 мм			аналог по характеристикам	шт.	1		пом. 1; крепление к стене; замена ≤ габарита
Кх15	Стол обеденный 1400×900, дуб табак; шпон, дуб натуральный, матовое масло; Ш×Г×В 1400×900×750 мм			аналог по характеристикам	шт.	1		пом. 1; замена ≤ габарита
Кх16	Стул обеденный к столу Кх15; обивка — ткань, цвет NCS S 1010-Y20R; каркас — дуб натуральный; Ш×Г×В 450×500×820 мм			аналог по характеристикам	шт.	6		пом. 1; замена ≤ габарита
Хл1**	Банкетка под окном, дуб табак; Ш×Г×В 1000×400×450 мм			аналог по характеристикам	шт.	1		пом. 2; замена ≤ габарита
Кб1**	Стол письменный у окна, дуб табак; шпон, дуб натуральный, матовое масло; Ш×Г×В 700×1600×750 мм			аналог по характеристикам	шт.	1		пом. 3; замена ≤ габарита
Кб2	Кресло рабочее; обивка — ткань, цвет NCS S 1010-Y20R; каркас — дуб натуральный; Ш×Г×В 600×600×900 мм			аналог по характеристикам	шт.	1		пом. 3; замена ≤ габарита
Кб3	Стеллаж для книг во всю стену; шпон, дуб натуральный, матовое масло; Ш×Г×В 2400×400×2400 мм			аналог по характеристикам	шт.	1		пом. 3; крепление к стене; замена ≤ габарита
Кб4	Кресло для чтения; обивка — ткань, цвет NCS S 1010-Y20R; Ш×Г×В 800×800×850 мм			аналог по характеристикам	шт.	1		пом. 3; замена ≤ габарита
Пх2	Банкетка-обувница; Ш×Г×В 1000×400×450 мм			аналог по характеристикам	шт.	1		пом. 5; замена ≤ габарита
М1	Кровать 1800×2000 с мягким изголовьем 1100, лён; мягкое изголовье, обивка — ткань, цвет NCS S 1010-Y20R; Ш×Г×В 1800×2100×1100 мм			аналог по характеристикам	шт.	1		пом. 6; замена ≤ габарита
М2, М3	Тумба прикроватная, дуб табак; шпон, дуб натуральный, матовое масло; Ш×Г×В 500×400×550 мм			аналог по характеристикам	шт.	2		пом. 6; замена ≤ габарита
М5	Комод, дуб табак; шпон, дуб натуральный, матовое масло; Ш×Г×В 1200×450×800 мм			аналог по характеристикам	шт.	1		пом. 6; крепление к стене; замена ≤ габарита
М6	Кресло у окна; обивка — ткань, цвет NCS S 1010-Y20R; Ш×Г×В 800×800×850 мм			аналог по характеристикам	шт.	1		пом. 6; замена ≤ габарита
Дт1, Дт6	Кровать 900×2000 с бортиком; мягкое изголовье, обивка — ткань, цвет NCS S 1010-Y20R; Ш×Г×В 900×2000×450 мм			аналог по характеристикам	шт.	2		пом. 7, 12; замена ≤ габарита
Дт2**	Стол письменный у окна; шпон, дуб натуральный, матовое масло; Ш×Г×В 1400×600×750 мм			аналог по характеристикам	шт.	1		пом. 7; замена ≤ габарита

Допущения и предложения на листе

Основа листа: взаимное расположение помещений, контур дома 9600 × 8000 и раскладка этажей подобраны проектировщиком под габариты помещений брифа; обмер и проект АР — задание (К-1); высота потолка 2900 мм — по брифу, не замерена; перекрытие 330 мм и отметка 2-го этажа +3,230 приняты; проект КР — задание (К-2); наружные стены 400 мм, перегородки 120 мм приняты (в брифе толщин нет) (К-1); разрешённая мощность 15 кВт принята по типовым ТУ для частного дома (К-4); подрайон климата не задан — принят не северный (жилые от 2,5 м) (К-7).

Знак «**» — предложение проектировщика, заказчиком не утверждено (согласовать с заказчиком): ИЗ-2: Хл1 — Было под окном стены А (700…1700) на радиаторе Рд3 (500…1700): прибор в корпусе; Кб1 — Было у стены В offset 400…2000 вплотную над радиатором Рд4 (750…1950): прибор в корпусе; Дт2 — Было у стены В offset 900…2300 над радиатором Рд6 (850…1850).

См. лист открытых вопросов (лист 7, записи К-1, К-2, К-4; лист 8, запись К-7; лист 9, запись ИЗ-2).

Изм.	Кол.уч	Лист	№ док.	Подп.	Дата
Разраб.		Кырлан А.С.			04.11.26
Пров.					
ГИП					
Н. контр.					
Утв.					

ГД-2026-012-АИ

Дом 120 м²

Общая площадь 147,36* м² · * размеры приняты, не замерены (реестр — л. 7–9, К-1)

Дизайн-проект интерьера

Стадия	Лист	Листов
РП	30	175

Спецификация мебели и оборудования (продолжение)

М б/м

Кырлан Александр Сергеевич

Спецификация мебели и оборудования (продолжение)

Форма 1 ГОСТ 21.110-2013 · позиции мебели — по плану расстановки

ПРЕДВАРИТЕЛЬНО · не для производства работ · открыто пунктов: 11 (реестр — л. 7–9)

Поз.	Наименование и техническая характеристика	Тип, марка, обозначение документа, опросного листа	Код продукции	Поставщик	Ед. измерения	Кол.	Масса 1 ед., кг	Примечание
Дт4, Дт9	Стул растущий; обивка — ткань, цвет NCS S 1010-Y20R; каркас — дуб натуральный; Ш×Г×В 500×500×800 мм			аналог по характеристикам	шт.	2		пом. 7, 12; замена ≤ габарита
Дт5	Стеллаж для книг и игрушек; шпон, дуб натуральный, матовое масло; Ш×Г×В 1200×300×1600 мм			аналог по характеристикам	шт.	1		пом. 7; крепление к стене; замена ≤ габарита
Хл2**	Стеллаж-библиотека низкий под окном; шпон, дуб натуральный, матовое масло; Ш×Г×В 900×350×850 мм			аналог по характеристикам	шт.	1		пом. 10; крепление к стене; замена ≤ габарита
Дт7**	Стол письменный у окна; шпон, дуб натуральный, матовое масло; Ш×Г×В 1200×600×750 мм			аналог по характеристикам	шт.	1		пом. 12; замена ≤ габарита
	Техника встраиваемая и бытовая (покупные изделия), светильники под розетки							
	Посудомоечная машина встраиваемая, в модуле Кх3; ниша 600 мм	аналог по характеристикам: полновстраиваемая 60 см под фасад, ниша 600 × 862 мм, навеска фасада в комплекте		по выбору заказчика до изготовления мебели	шт.	1		пом. 1; по схеме изготовителя
	Варочная панель встраиваемая, индукционная, в модуле Кх7	аналог по характеристикам: индукционная 60 см, вырез 560 × 490 мм по шаблону модели		по выбору заказчика до изготовления мебели	шт.	1		пом. 1; по схеме изготовителя
	Духовой шкаф встраиваемый, в модуле Кх7	аналог по характеристикам: 60 см, лицевая панель 595 мм, ниша 560 × 600, глубина ≥ 550 мм, вентиляция за прибором		по выбору заказчика до изготовления мебели	шт.	1		пом. 1; по схеме изготовителя
	Холодильник встраиваемый, в модуле Кх9	аналог по характеристикам: полновстраиваемый под фасад, ниша 1780 × 560 × 550 мм, вентиляция решётка в цоколе, выход сверху		по выбору заказчика до изготовления мебели	шт.	1		пом. 1; по схеме изготовителя
	Вытяжка встраиваемая, в модуле Кх13	аналог по характеристикам: производительность — по расчёту ОВ, шум ≤ 55 дБ(А)		по выбору заказчика до изготовления мебели	шт.	1		пом. 1; по схеме изготовителя
	Стиральная машина, место по листу ВК (См3**); Ш×Г 600×600 мм	аналог по характеристикам: тип загрузки — по листу ВК, в плане 600 × 600 мм (ширина × глубина), по листу ВК		по выбору заказчика до изготовления мебели	шт.	1		пом. 13; по схеме изготовителя
	Торшер, у поз. Гс4; абажур — ткань или опаловое стекло; лампа 2700 K			аналог по характеристикам	шт.	1		пом. 1; розетка Р21 (ЭОМ)
	Лампа настольная, у поз. Кб1**; абажур — ткань или опаловое стекло; лампа 2700 K			аналог по характеристикам	шт.	1		пом. 3; розетка Р9 (ЭОМ)
	Лампа настольная, у поз. Кб1**; абажур — ткань или опаловое стекло; лампа 2700 K			аналог по характеристикам	шт.	1		пом. 3; розетка Р10 (ЭОМ)
	Торшер, у поз. Кб3; абажур — ткань или опаловое стекло; лампа 2700 K			аналог по характеристикам	шт.	1		пом. 3; розетка Р11 (ЭОМ)
	Торшер, у поз. М6; абажур — ткань или опаловое стекло; лампа 2700 K			аналог по характеристикам	шт.	1		пом. 6; розетка Р5 (ЭОМ)
	Лампа настольная, у поз. Дт2**; абажур — ткань или опаловое стекло; лампа 2700 K			аналог по характеристикам	шт.	1		пом. 7; розетка Р42 (ЭОМ)
	Лампа настольная, у поз. Дт7**; абажур — ткань или опаловое стекло; лампа 2700 K			аналог по характеристикам	шт.	1		пом. 12; розетка Р47 (ЭОМ)
	Текстиль							
Т13	Портьеры-волна (гостиная); лён 70 %, вискоза 30 %; цвет NCS S 1010-Y20R; карниз 3000 мм, высота 2790 мм, сборка 2			аналог по характеристикам	шт.	2		пом. 1
Т14	Тюль (гостиная); полиэстер 100 %; цвет Little Greene No. 222; карниз 3000 мм, высота 2790 мм, сборка 2,5			аналог по характеристикам	шт.	1		пом. 1

Допущения и предложения на листе

Основа листа: взаимное расположение помещений, контур дома 9600 × 8000 и раскладка этажей подобраны проектировщиком под габариты помещений брифа; обмер и проект АР — задание (К-1); высота потолка 2900 мм — по брифу, не замерена; перекрытие 330 мм и отметка 2-го этажа +3,230 приняты; проект КР — задание (К-2); наружные стены 400 мм, перегородки 120 мм приняты (в брифе толщин нет) (К-1); разрешённая мощность 15 кВт принята по типовым ТУ для частного дома (К-4); подрайон климата не задан — принят не северный (жилые от 2,5 м) (К-7).

Знак «**» — предложение проектировщика, заказчиком не утверждено (согласовать с заказчиком): ИЗ-1: См3 — Было у стены Г offset 300 — пересекалась с умывальником См4 в углу А/Г, люк упирался в раковину; ИЗ-2: Кб1 — Было у стены В offset 400…2000 вплотную над радиатором Рд4 (750…1950): прибор в корпусе; Дт2 — Было у стены В offset 900…2300 над радиатором Рд6 (850…1850); Хл2 — Было под окном стены А (700…1600) перед радиатором Рд7 (500…1700); Дт7 — Было у стены В offset 600…1800 над радиатором Рд8 (800…1800). См. лист открытых вопросов (лист 7, записи К-1, К-2, К-4; лист 8, запись К-7; лист 9, записи ИЗ-1, ИЗ-2).

Изм.	Кол.уч	Лист	№ док.	Подп.	Дата
Разраб.		Кырлан А.С.			04.11.26
Пров.					
ГИП					
Н. контр.					
Утв.					

ГД-2026-012-АИ

Дом 120 м²

Общая площадь 147,36* м² · * размеры приняты, не замерены (реестр — л. 7–9, К-1)

Дизайн-проект интерьера

Стадия	Лист	Листов
РП	31	175

Спецификация мебели и оборудования (продолжение)

М б/м

Кырлан Александр Сергеевич

Спецификация мебели и оборудования (продолжение)

ПРЕДВАРИТЕЛЬНО · не для производства работ · открыто пунктов: 11 (реестр — л. 7–9)

Форма 1 ГОСТ 21.110-2013 · позиции мебели — по плану расстановки

Поз.	Наименование и техническая характеристика	Тип, марка, обозначение документа, опросного листа	Код продукции	Поставщик	Ед. измерения	Кол.	Масса 1 ед., кг	Примечание
T15	Римская штора (кухня); лён 100 %; цвет Tikkurila X463; карниз 1500 мм, высота 1600 мм			аналог по характеристикам	шт.	1		пом. 1
T16	Ковёр в зоне отдыха; шерсть 100 %; цвет Tikkurila X463; 2400×2000 мм			аналог по характеристикам	шт.	1		пом. 1; с подложкой
T17	Подушки на диван; букле (шерсть 60 %, полиэстер 40 %); цвет NCS S 1010-Y20R			аналог по характеристикам	шт.	3		пом. 1
T18	Подушки на диван, акцент; хлопковый бархат 100 %; цвет NCS S 3050-R80B			аналог по характеристикам	шт.	2		пом. 1
T19	Плед на диван; альпака 50 %, шерсть 50 %; цвет Tikkurila X463			аналог по характеристикам	шт.	1		пом. 1
T7	Портьеры-волна; лён 100 %; цвет NCS S 1010-Y20R; карниз 2100 мм, высота 2890 мм, сборка 2			аналог по характеристикам	шт.	2		пом. 3
T8	Тюль; полиэстер 100 %; цвет Little Greene No. 222; карниз 2100 мм, высота 2890 мм, сборка 2,5			аналог по характеристикам	шт.	1		пом. 3
T9	Ковёр под кроватью; шерсть 100 %; цвет Tikkurila X463; 2000×1500 мм			аналог по характеристикам	шт.	1		пом. 3; с подложкой
T10	Подушки декоративные на кровать; букле (шерсть 60 %, полиэстер 40 %); цвет NCS S 1010-Y20R			аналог по характеристикам	шт.	3		пом. 3
T11	Подушки на кровать, акцент; хлопковый бархат 100 %; цвет NCS S 5020-G90Y			аналог по характеристикам	шт.	2		пом. 3
T12	Плед на кровать; шерсть мериноса 100 %; цвет NCS S 5020-G90Y			аналог по характеристикам	шт.	1		пом. 3
T1	Портьеры-волна; лён 100 %; цвет NCS S 1010-Y20R; карниз 2400 мм, высота 2890 мм, сборка 2			аналог по характеристикам	шт.	2		пом. 6
T2	Тюль; полиэстер 100 %; цвет Little Greene No. 222; карниз 2400 мм, высота 2890 мм, сборка 2,5			аналог по характеристикам	шт.	1		пом. 6
T3	Ковёр под кроватью; шерсть 80 %, хлопок 20 %; цвет Tikkurila X395; 2200×2700 мм			аналог по характеристикам	шт.	1		пом. 6; с подложкой
T4	Подушки декоративные на кровать; лён 100 %; цвет NCS S 1010-Y20R			аналог по характеристикам	шт.	3		пом. 6
T5	Подушки на кровать, акцент; хлопковый бархат 100 %; цвет Farrow & Ball No. 89			аналог по характеристикам	шт.	2		пом. 6
T6	Плед на кровать; шерсть мериноса 100 %; цвет Farrow & Ball No. 89			аналог по характеристикам	шт.	1		пом. 6
T20	Портьеры-волна; лён 100 %; цвет NCS S 1010-Y20R; карниз 2100 мм, высота 2790 мм, сборка 2			аналог по характеристикам	шт.	2		пом. 7
T21	Тюль; полиэстер 100 %; цвет Little Greene No. 222; карниз 2100 мм, высота 2790 мм, сборка 2,5			аналог по характеристикам	шт.	1		пом. 7
T22	Ковёр под кроватью; шерсть 100 %; цвет Tikkurila X463; 1350×1900 мм			аналог по характеристикам	шт.	1		пом. 7; с подложкой
T23	Подушки декоративные на кровать; букле (шерсть 60 %, полиэстер 40 %); цвет NCS S 1010-Y20R			аналог по характеристикам	шт.	3		пом. 7
T24	Подушки на кровать, акцент; хлопковый бархат 100 %; цвет Farrow & Ball No. 66			аналог по характеристикам	шт.	2		пом. 7
T25	Плед на кровать; шерсть мериноса 100 %; цвет Farrow & Ball No. 66			аналог по характеристикам	шт.	1		пом. 7
T26	Портьеры-волна; лён 100 %; цвет NCS S 1010-Y20R; карниз 2000 мм, высота 2790 мм, сборка 2			аналог по характеристикам	шт.	2		пом. 12
T27	Тюль; полиэстер 100 %; цвет Little Greene No. 222; карниз 2000 мм, высота 2790 мм, сборка 2,5			аналог по характеристикам	шт.	1		пом. 12
T28	Ковёр под кроватью; шерсть 100 %; цвет Tikkurila X463; 1350×1900 мм			аналог по характеристикам	шт.	1		пом. 12; с подложкой
T29	Подушки декоративные на кровать; букле (шерсть 60 %, полиэстер 40 %); цвет NCS S 1010-Y20R			аналог по характеристикам	шт.	3		пом. 12
T30	Подушки на кровать, акцент; хлопковый бархат 100 %; цвет Tikkurila H440			аналог по характеристикам	шт.	2		пом. 12

Допущения и предложения на листе

Основа листа: взаимное расположение помещений, контур дома 9600 × 8000 и раскладка этажей подобраны проектировщиком под габариты помещений брифа; обмер и проект АР — задание (К-1); высота потолка 2900 мм — по брифу, не замерена; перекрытие 330 мм и отметка 2-го этажа +3,230 приняты; проект КР — задание (К-2); наружные стены 400 мм, перегородки 120 мм приняты (в брифе толщин нет) (К-1); разрешённая мощность 15 кВт принята по типовым ТУ для частного дома (К-4); подрайон климата не задан — принят не северный (жилые от 2,5 м) (К-7).

См. лист открытых вопросов (лист 7, записи К-1, К-2, К-4; лист 8, запись К-7).

Изм.	Кол.уч	Лист	№ док.	Подп.	Дата
Разраб.		Кырлан А.С.			04.11.26
Пров.					
ГИП					
Н. контр.					
Утв.					

ГД-2026-012-АИ

Дом 120 м²

Общая площадь 147,36* м² · * размеры приняты, не замерены (реестр — л. 7–9, К-1)

	Стадия	Лист	Листов
Дизайн-проект интерьера	РП	32	175
Спецификация мебели и оборудования (продолжение) М б/м	**Кырлан Александр Сергеевич**		

Спецификация мебели и оборудования (продолжение)

Форма 1 ГОСТ 21.110-2013 · позиции мебели — по плану расстановки

ПРЕДВАРИТЕЛЬНО · не для производства работ · открыто пунктов: 11 (реестр — л. 7–9)

Поз.	Наименование и техническая характеристика	Тип, марка, обозначение документа, опросного листа	Код продукции	Поставщик	Ед. измерения	Кол.	Масса 1 ед., кг	Примечание
Т31	Плед на кровать; шерсть мериноса 100 %; цвет Tikkurila H440			аналог по характеристикам	шт.	1		пом. 12
	Декор							
ДК6	Картина над креслом: пейзаж, масло, рама — дуб табак; 1000×800 мм; центр на 1550 мм от пола			аналог по характеристикам	шт.	1	6	пом. 1; крепление: анкер, 2 шт.
ДК7	Растение в кашпо; 450×450 мм			аналог по характеристикам	шт.	1		пом. 1
ДК8	Ваза керамическая с ветками на обеденном столе; 200×350 мм; на Кх15			аналог по характеристикам	шт.	1		пом. 1
ДК40	Олива в кадке Ø450 у окна; 450×450 мм			аналог по характеристикам	шт.	1		пом. 1
ДК41	Сансевиерия в кашпо Ø400 под лестницей; 400×400 мм			аналог по характеристикам	шт.	1		пом. 2
ДК3	Картина над креслом: гравюра в паспарту, рама — графит; 550×450 мм; низ на 1050 мм от пола			аналог по характеристикам	шт.	1	4	пом. 3; крепление к стене
ДК9	Зеркало над умывальником, влагостойкое; 500×700 мм; низ на 1100 мм от пола			аналог по характеристикам	шт.	1	4	пом. 4; крепление к стене
ДК5	Зеркало; рама — чёрный матовый; 600×1800 мм; низ на 550 мм от пола			аналог по характеристикам	шт.	1	18	пом. 5; крепление: анкер, 4 шт.
ДК43	Замиокулькас в кашпо Ø350; 350×350 мм			аналог по характеристикам	шт.	1		пом. 5
ДК1	Картина над кроватью: акварель, рама — светлый дуб; 1000×700 мм; низ на 1300 мм от пола			аналог по характеристикам	шт.	1	4	пом. 6; крепление к стене
ДК44	Аглаонема в кашпо Ø400; 400×400 мм			аналог по характеристикам	шт.	1		пом. 6
ДК2	Картина над кроватью: детская иллюстрация, рама — белёный дуб; 600×450 мм; низ на 650 мм от пола			аналог по характеристикам	шт.	1	4	пом. 7; крепление к стене
ДК4	Зеркало в рост в тонкой чёрной раме; рама — чёрный матовый; 500×1600 мм; низ на 300 мм от пола			аналог по характеристикам	шт.	1	12	пом. 7; крепление: анкер для пустотелых оснований, 4 шт.
ДК45	Хлорофитум в кашпо Ø350 у окна; 350×350 мм			аналог по характеристикам	шт.	1		пом. 10
ДК46	Сансевиерия в кашпо Ø400; 400×400 мм			аналог по характеристикам	шт.	1		пом. 11
ДК10	Картина над кроватью: детский принт, рама — светлый ясень; 600×450 мм; низ на 650 мм от пола			аналог по характеристикам	шт.	1	4	пом. 12; крепление к стене
ДК11	Зеркало в рост в тонкой чёрной раме; рама — чёрный матовый; 500×1600 мм; низ на 300 мм от пола			аналог по характеристикам	шт.	1	12	пом. 12; крепление: анкер для пустотелых оснований, 4 шт.
ДК12	Зеркало над умывальником, влагостойкое; 600×750 мм; низ на 1100 мм от пола			аналог по характеристикам	шт.	1	4	пом. 13; крепление к стене

Допущения и предложения на листе

Основа листа: взаимное расположение помещений, контур дома 9600 × 8000 и раскладка этажей подобраны проектировщиком под габариты помещений брифа; обмер и проект АР — задание (К-1); высота потолка 2900 мм — по брифу, не замерена; перекрытие 330 мм и отметка 2-го этажа +3,230 приняты; проект КР — задание (К-2); наружные стены 400 мм, перегородки 120 мм приняты (в брифе толщин нет) (К-1); разрешённая мощность 15 кВт принята по типовым ТУ для частного дома (К-4); подрайон климата не задан — принят не северный (жилые от 2,5 м) (К-7).

См. лист открытых вопросов (лист 7, записи К-1, К-2, К-4; лист 8, запись К-7).

Изм.	Кол.уч	Лист	№ док.	Подп.	Дата
Разраб.		Кырлан А.С.			04.11.26
Пров.					
ГИП					
Н. контр.					
Утв.					

ГД-2026-012-АИ

Дом 120 м²

Общая площадь 147,36* м² · * размеры приняты, не замерены (реестр — л. 7–9, К-1)

Дизайн-проект интерьера

Стадия	Лист	Листов
РП	33	175

Спецификация мебели и оборудования (продолжение)


М б/м

Кырлан Александр Сергеевич

План розеток и электровыводов · 1-й этаж

Розетки, выводы кабеля, щит · размеры в мм · высоты от чистого пола

ПРЕДВАРИТЕЛЬНО · не для производства работ · открыто пунктов: 11 (реестр — л. 7–9)

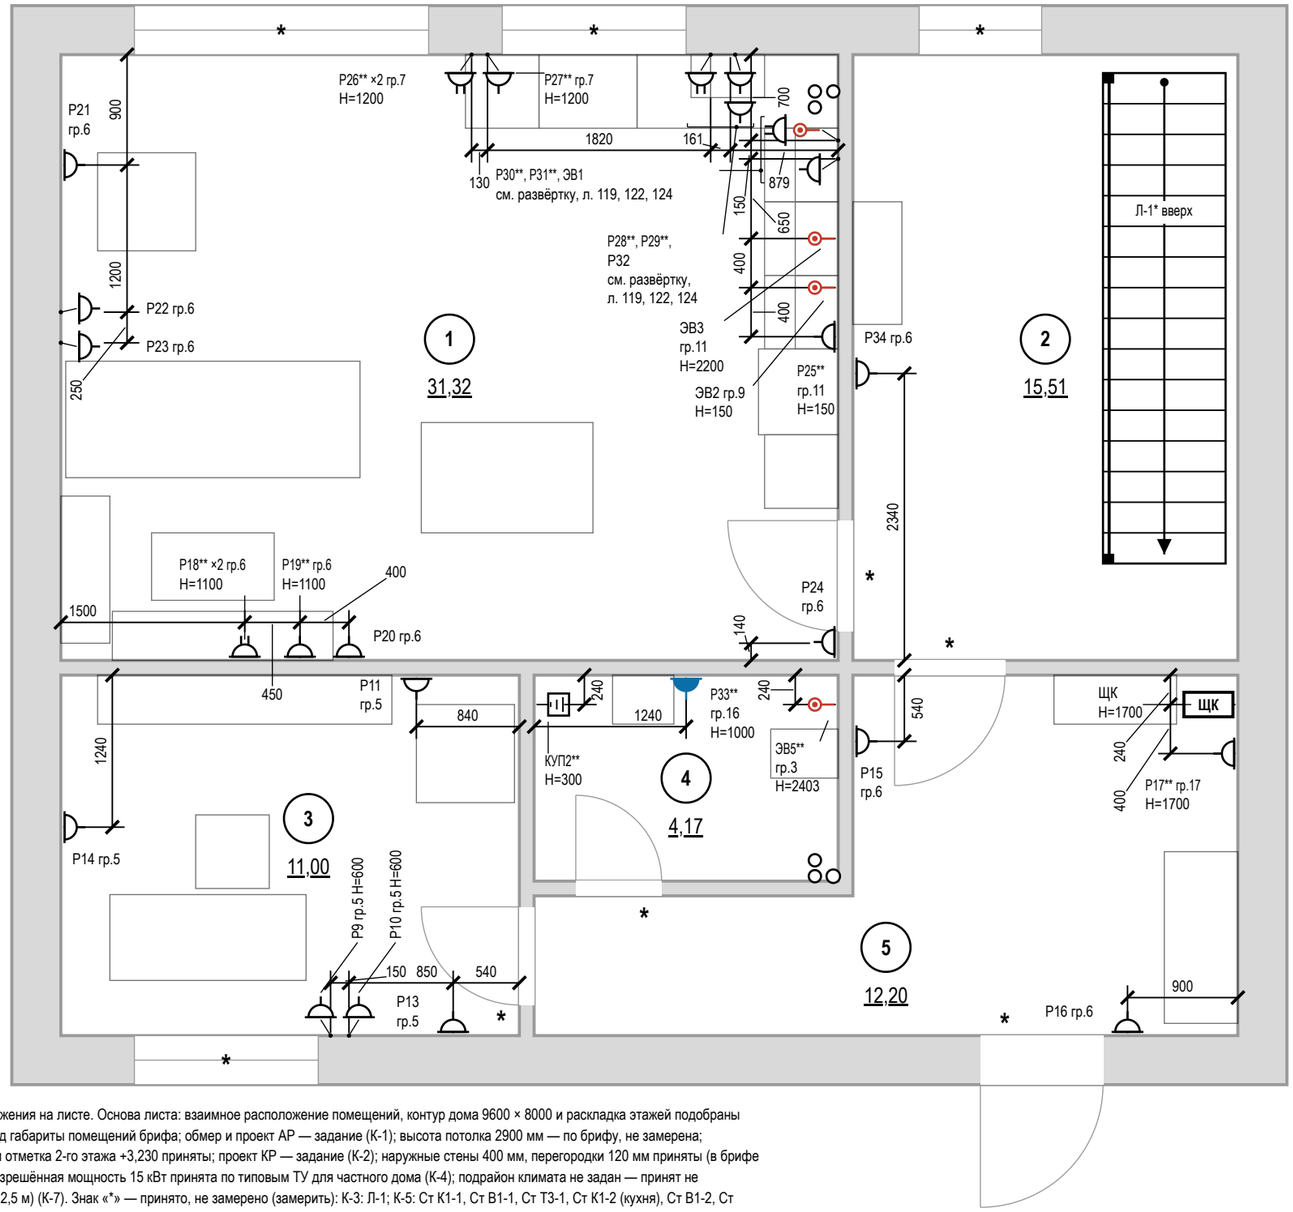

Допущения и предложения на листе. Основа листа: взаимное расположение помещений, контур дома 9600 × 8000 и раскладка этажей подобраны проектировщиком под габариты помещений брифа; обмер и проект АР — задание (К-1); высота потолка 2900 мм — по брифу, не замерена; перекрытие 330 мм и отметка 2-го этажа +3,230 приняты; проект КР — задание (К-2); наружные стены 400 мм, перегородки 120 мм приняты (в брифе толщин нет) (К-1); разрешённая мощность 15 кВт принята по типовым ТУ для частного дома (К-4); подрайон климата не задан — принят не северный (жилые от 2,5 м) (К-7). Знак «*» — принято, не замерено (замерить): К-3: Л-1; К-5: Ст К1-1, Ст В1-1, Ст Т3-1, Ст К1-2 (кухня), Ст В1-2, Ст Т3-2. Знак «**» — предложено, не утверждено (согласовать): Р18, Р19, Р25, Р26, Р27, Р28, Р29, Р30, Р31, ЭВ5, КУП2; ИЗ-2: Р33, Р17. См. лист открытых вопросов (лист 7, записи К-1–К-5; лист 8, запись К-7; лист 9, записи ИЗ-1, ИЗ-2).

Условные обозначения

Знак	Тип изделия	H, мм	Кол., шт
	Розетка с заземлением	300	12
	То же	у знака	8
	Блок розеток с заземлением, рамка 2 поста	у знака	4
	Розетка с заземлением IP44	1000	1
	Вывод кабеля к прибору	у знака	4
	КУП (уравнивание потенциалов)	300	1
ЩК	Щит квартирный	1700	1

розетка с заземляющим контактом; у знака — марка, ×N — постов в рамке, гр. — группа щита, H — высота оси, мм

знак разведён для читаемости: точка на стене — у выноски, привязка — до неё

мебель и сантехприборы — подложка

стояк: К1 — канализация, В1 — ХВС, Т3 — ГВС

1 — номер помещения, площадь м²

Итого розеток (механизмов) — 29 шт; рамок — 25 шт: на 1 пост — 21, на 2 поста — 4.

Примечания

1. За отметку 0,000 принят уровень чистого пола. Высоты H — от чистого пола до оси изделия; привязки — от чистовой грани стены до оси механизма (у рамки на несколько постов — до оси рамки).
2. Розетки без отметки H у знака — на высоте 300 мм от чистого пола до оси механизма; выводы кабеля — по паспорту прибора.
3. Розетки в санузле — только вне зон 0–2 (ПУЭ 7.1.48, ГОСТ Р 50571.7.701-2024), IP44, через УЗО 30 мА.
4. Розеточные и мокрые линии — через УЗО или дифавтомат с током утечки не более 30 мА (ПУЭ 7.1.79); в санузле выполнить ДСУП (ПУЭ 7.1.87–7.1.88).
5. Кабель — медный, исполнение нг(A)-LS (ГОСТ 31565-2012); скрытая прокладка только горизонтально и вертикально, фактические трассы зафиксировать исполнительной схемой до закрытия отделкой.
6. Расчёт нагрузок, токов КЗ, селективности и сечений — по проекту ЭОМ организации с допуском СРО; лист задаёт состав, расположение и группы.
7. Выводы кухонной техники — после утверждения проекта кухни (ориентировочно); привязки выводов даны от осей модулей гарнитура и пересматриваются вместе с проектом кухни.
8. Электрический тёплый пол проектом не предусмотрен; при решении заказчика устроить — отдельный лист «План тёплых полов»: контуры с отступом 100 мм от стен и мебели без ножек, датчик в гофре, терморегулятор, своя группа щита через УЗО 30 мА.
9. Ведомости электроточек, изделий, светильников и расшифровка клавиш — лист 40.

1000 мм · печать 1:1

Изм.	Кол.уч	Лист	№ док.	Подп.	Дата
Разраб.		Кырлан А.С.			04.11.26
Пров.					
ГИП					
Н. контр.					
Утв.					

ГД-2026-012-АИ

Дом 120 м²

Общая площадь 147,36* м² · * размеры приняты, не замерены (реестр — л. 7–9, К-1)

	Стадия	Лист	Листов
Дизайн-проект интерьера	РП	34	175

План розеток и электровыводов · 1-й этаж

М 1:50


Кырлан Александр Сергеевич

выпуск 04.11.2026 № 4dfa962484 · стр. 35 из 180

План розеток и электровыводов · 2-й этаж

Розетки, выводы кабеля, щит · размеры в мм · высоты от чистого пола

ПРЕДВАРИТЕЛЬНО · не для производства работ · открыто пунктов: 11 (реестр — л. 7–9)

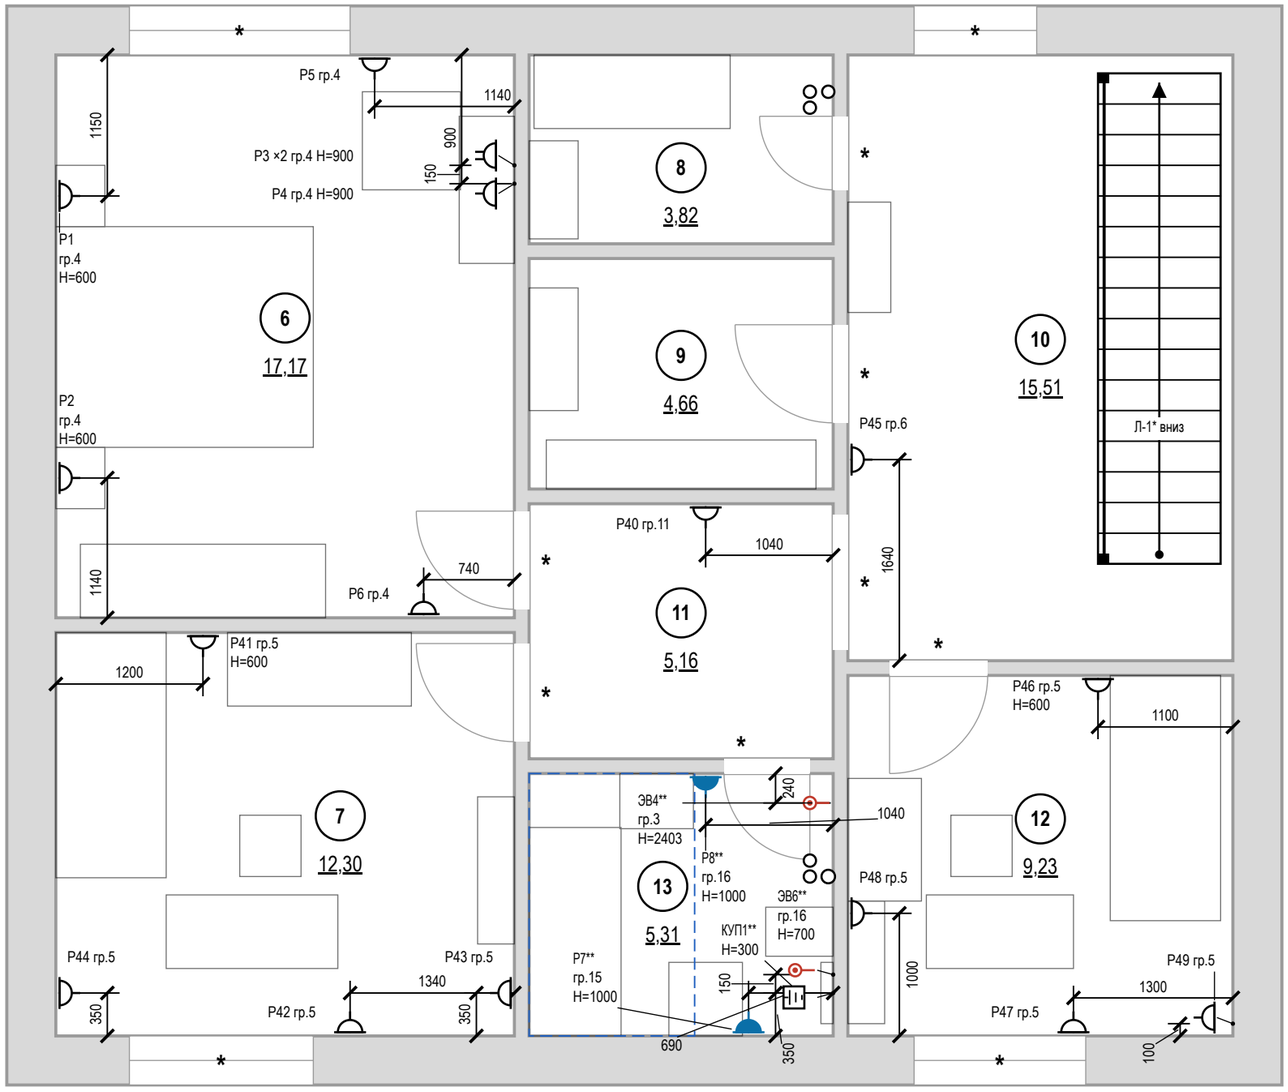

Условные обозначения

Знак	Тип изделия	Н, мм	Кол., шт
	Розетка с заземлением	300	10
	То же	у знака	5
	Блок розеток с заземлением, рамка 2 поста	900	1
	Розетка с заземлением IP44	1000	2
	Вывод кабеля к прибору	у знака	2
	КУП (уравнивание потенциалов)	300	1

розетка с заземляющим контактом; у знака — марка, ×N — постов в рамке, гр. — группа щита, Н — высота оси, мм

знак разведён для читаемости: точка на стене — у выноски, привязка — до неё

граница зоны 2 ванной (600 мм от ванны/поддона)

мебель и сантехприборы — подложка

стояк: К1 — канализация, В1 — ХВС, Т3 — ГВС

1 — номер помещения, площадь м²

Итого розеток (механизмов) — 19 шт; рамок — 18 шт: на 1 пост — 17, на 2 поста — 1.

Допущения и предложения на листе

Основа листа: взаимное расположение помещений, контур дома 9600 × 8000 и раскладка этажей подобраны проектировщиком под габариты помещений брифа; обмер и проект АР — задание (К-1); высота потолка 2900 мм — по брифу, не замерена; перекрытие 330 мм и отметка 2-го этажа +3,230 приняты; проект КР — задание (К-2); наружные стены 400 мм, перегородки 120 мм приняты (в брифе толщин нет) (К-1); разрешённая мощность 15 кВт принята по типовым ТУ для частного дома (К-4); подрайон климата не задан — принят не северный (жилые от 2,5 м) (К-7).

Знак «*» — принято, не замерено и не подтверждено (замерить на объекте): К-1: окно пом. 6 (стена А), 7 (В), 10 (А), 12 (В) — окно: место, ширина, высота и подоконник приняты по брифу, стена — по раскладке проектировщика (К-1), не замерены; дверь пом. 6 (стена Б), 7 (Б), 8 (Б), 9 (Б), 11 (Б), 12 (А) — проём: место и ширина приняты проектировщиком по брифу (раскладка этажей — К-1), не замерены; дверь пом. 13 (стена А) — Петли у правого откоса (х 6150, у стояков): открытое полотно стоит вдоль стены Б, вошедший идёт влево к умывальнику и ванне; К-2: отметка чистого пола этажа «2-й этаж» +3,230 — отметка чистого пола 2-го этажа +3,230 принята: высота потолка 2900 по брифу + перекрытие с полом 330 (конструкция перекрытия не задана; проект КР — задание); К-3: Л-1 — место, тип и размеры лестницы брифом не заданы (только «лестница из холла 1-го этажа»): одномаршевая 17 × 190 × 250 вдоль стены Б холла — предложение проектировщика; конструкция и расчёт — проект КР; К-5: Ст К1-1, Ст В1-1, Ст Т3-1, Ст К1-2 (кухня), Ст В1-2, Ст Т3-2 — положение стояка принято проектировщиком (проект ВК дома не передан), не замерено.

Знак «**» — предложение проектировщика, заказчиком не утверждено (согласовать с заказчиком): ЭВ4 — Вентилятор ВР1 на стене Б у потолка, offset 300 (над зоной входа); ИЗ-1: КУП1 — КУП за унитазом См2 (1150…1550) ниже — offset 1850, Н=300; ИЗ-1, ИЗ-2: Р7 — Розетка стиральной машины — за машиной См3 (стена В, 1200…1800), Н=1000, вне зон 0–2 ванны (ванна у стены Г до х 4550); Р8 — Фен у умывальника См4 (800…1400 на стене А): справа от раковины, до откоса проёма Д-8 (1650) — 150 мм; ЭВ6 — Вывод полотенцесушителя См5 (стена Б, 1600…2100).

Открытые вопросы и конфликты по листу: К-4.

Изменения по листу без подписи: ИЗ-1, ИЗ-2.

См. лист открытых вопросов (лист 7, записи К-1–К-5; лист 8, запись К-7; лист 9, записи ИЗ-1, ИЗ-2).

Примечания

1. За отметку 0,000 принят уровень чистого пола. Высоты Н — от чистого пола до оси изделия; привязки — от чистовой грани стены до оси механизма (у рамки на несколько постов — до оси рамки).
2. Розетки без отметки Н у знака — на высоте 300 мм от чистого пола до оси механизма; выводы кабеля — по паспорту прибора.
3. Розетки в санузле — только вне зон 0–2 (ПУЭ 7.1.48, ГОСТ Р 50571.7.701-2024), IP44, через УЗО 30 мА.
4. Розеточные и мокрые линии — через УЗО или дифавтомат с током утечки не более 30 мА (ПУЭ 7.1.79); в санузле выполнить ДСУП (ПУЭ 7.1.87–7.1.88).
5. Кабель — медный, исполнение нг(А)-LS (ГОСТ 31565-2012); скрытая прокладка только горизонтально и вертикально, фактические трассы зафиксировать исполнительной схемой до закрытия отделкой.
6. Расчёт нагрузок, токов КЗ, селективности и сечений — по проекту ЭОМ организации с допуском СРО; лист задаёт состав, расположение и группы.
7. Электрический тёплый пол проектом не предусмотрен; при решении заказчика устроить — отдельный лист «План тёплых полов»: контуры с отступом 100 мм от стен и мебели без ножек, датчик в гофре, терморегулятор, своя группа щита через УЗО 30 мА.
8. Ведомости электроточек, изделий, светильников и расшифровка клавиш — лист 40.

1000 мм · печать 1:1

Изм.	Кол.уч	Лист	№ док.	Подп.	Дата
Разраб.		Кырлан А.С.			04.11.26
Пров.					
ГИП					
Н. контр.					
Утв.					

ГД-2026-012-АИ

Дом 120 м²

Общая площадь 147,36* м² · * размеры приняты, не замерены (реестр — л. 7–9, К-1)

Дизайн-проект интерьера

Стадия	Лист	Листов
РП	35	175

План розеток и электровыводов · 2-й этаж

М 1:50


Кырлан Александр Сергеевич

выпуск 04.11.2026 № 4dfa962484 · стр. 36 из 180

План освещения · 1-й этаж

Светильники, группы включения, извещатели · размеры в мм

ПРЕДВАРИТЕЛЬНО · не для производства работ · открыто пунктов: 11 (реестр — л. 7–9)

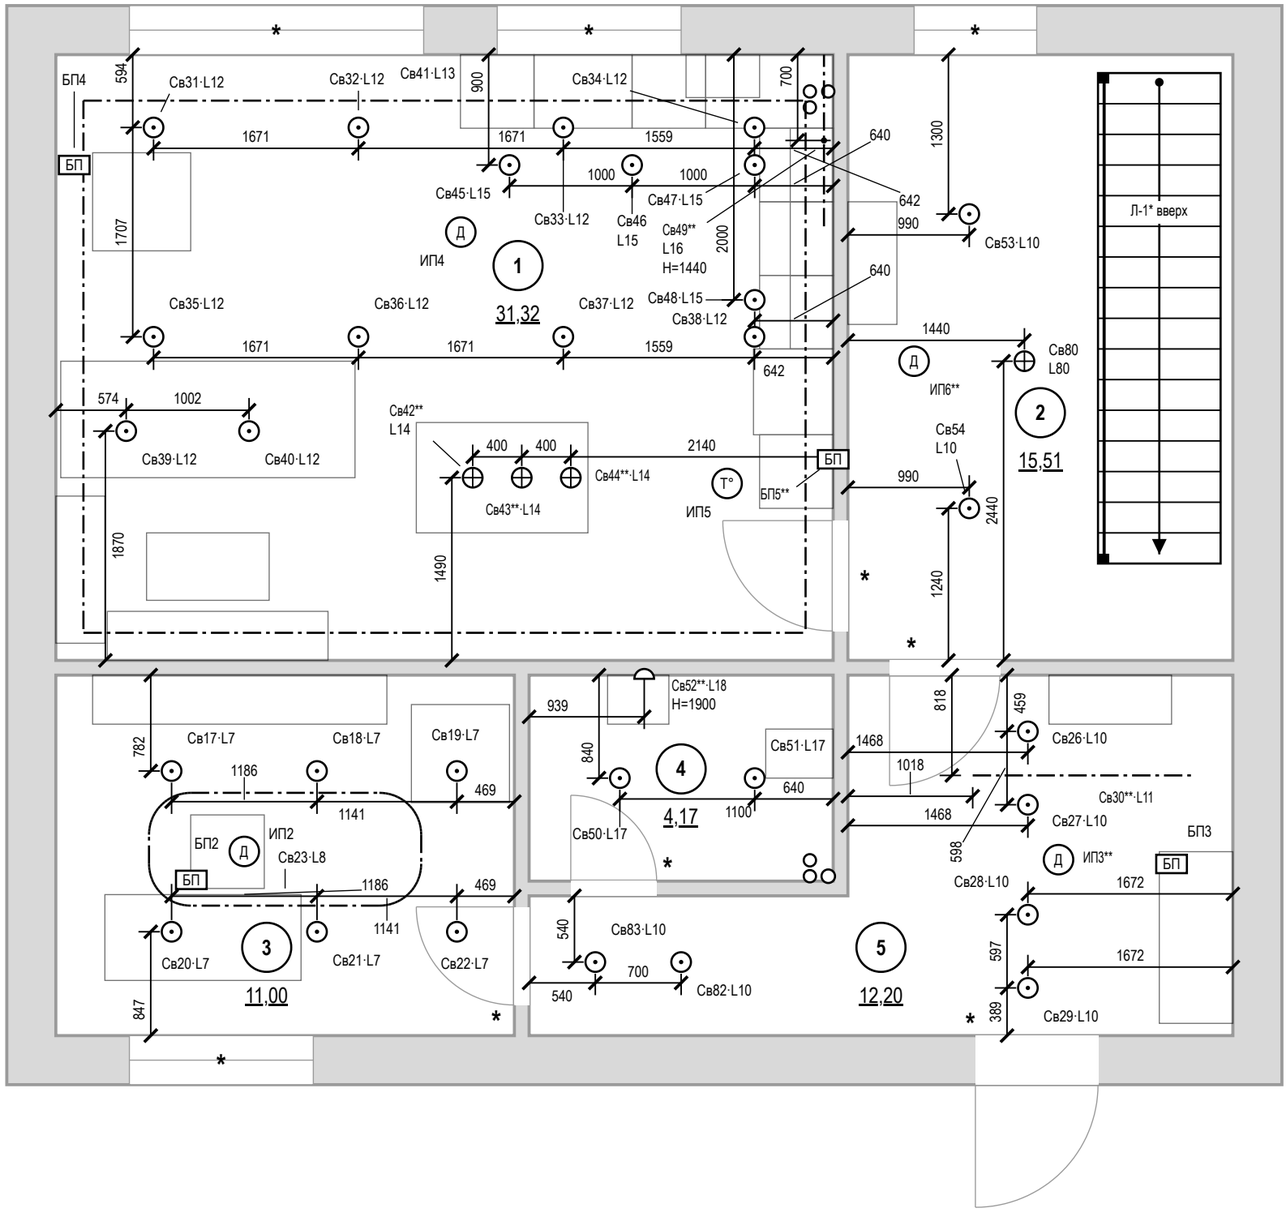

Условные обозначения

- светильник встраиваемый точечный
- светильник подвесной
- светильник настенный (бра), H — высота оси
- линейный светильник настенный (подсветка столешницы), точка — вывод питания
- светодиодная лента в профиле / в карнизе короба
- Св1·L1 — марка светильника (как в ведомости и на развёртках) · группа включения L (лист 38)
- Д — извещатель пожарный дымовой автономный
- Т° — извещатель пожарный тепловой
- БП — блок питания LED, с доступом (люк от 100×100 мм)
- мебель и сантехприборы — подложка
- стояк: К1 — канализация, В1 — ХВС, Т3 — ГВС
- 1 — номер помещения, площадь м²

Допущения и предложения на листе

Основа листа: взаимное расположение помещений, контур дома 9600 × 8000 и раскладка этажей подобраны проектировщиком под габариты помещений брифа; обмер и проект АР — задание (К-1); высота потолка 2900 мм — по брифу, не замерена; перекрытие 330 мм и отметка 2-го этажа +3,230 приняты; проект КР — задание (К-2); наружные стены 400 мм, перегородки 120 мм приняты (в брифе толщин нет) (К-1); разрешённая мощность 15 кВт принята по типовым ТУ для частного дома (К-4); подрайон климата не задан — принят не северный (жилые от 2,5 м) (К-7).

Знак «*» — принято, не замерено и не подтверждено (замерить на объекте): К-1: окно пом. 1 (стена А), 2 (А), 3 (В) — окно: место, ширина, высота и подоконник приняты по брифу, стена — по раскладке проектировщика (К-1), не замерены; дверь пом. 1 (стена Б), 3 (Б), 4 (В), 5 (А) — проём: место и ширина приняты проектировщиком по брифу (раскладка этажей — К-1), не замерены; дверь пом. 5 (стена В) — входная дверь: место и ширина проёма приняты проектировщиком по брифу (без плана дома), не замерены; К-3: Л-1 — место, тип и размеры лестницы брифом не заданы (только «лестница из холла 1-го этажа»): одномаршевая 17 × 190 × 250 вдоль стены Б холла — предложение проектировщика; конструкция и расчёт — проект КР; К-5: Ст К1-1, Ст В1-1, Ст Т3-1, Ст К1-2 (кухня), Ст В1-2, Ст Т3-2 — положение стояка принято проектировщиком (проект ВК дома не передан), не замерено.

Знак «**» — предложение проектировщика, заказчиком не утверждено (согласовать с заказчиком): Св42, Св43, Св44, Св49, БП5 — диммируемость добавлена разработчиком проекта под светорегуляторы S10 и S11; ИП6, ИП3 — дымовой автономный вместо теплового образца: жилой дом — автономные дымовые в путях эвакуации (СП 486, пункт сверить по действующей редакции); Св52 — Сдвиг под раскладку плитки стены А на 49 мм вдоль стены — ось на шве или в центре плитки, привязка по таблице листа; Св30 — открытая лента в накладном профиле вместо «в коробе»: короба в потолке нет — подвесной потолок помещения без короба и ниши LED.

См. лист открытых вопросов (лист 7, записи К-1–К-5; лист 8, запись К-7).

Примечания

1. За отметку 0,000 принят уровень чистого пола. Высоты H — от чистого пола до оси изделия; привязки — от чистовой грани стены до оси механизма (у рамки на несколько постов — до оси рамки).
2. Высота установки, не указанная на плане: светильники — на потолке; настенные — по отметке H у знака. Привязки — до оси светильника от чистовой грани стены, по рядам.
3. Во влажных помещениях — светильники не ниже IP44; в зонах 0–2 ванной — по ГОСТ Р 50571.7.701-2024 (зона 1 — IPX5).
4. LED-лента в карнизе подсветки короба — по линии карниза с плана потолков; блок питания — в люке короба (БП на плане), питание ленты длиннее 5 м — с двух концов.
5. Розеточные и мокрые линии — через УЗО или дифавтомат с током утечки не более 30 мА (ПУЭ 7.1.79); в санузле выполнить ДСУП (ПУЭ 7.1.87–7.1.88).
6. Кабель — медный, исполнение нг(А)-LS (ГОСТ 31565-2012); скрытая прокладка только горизонтально и вертикально, фактические трассы зафиксировать исполнительной схемой до закрытия отделкой.
7. Расчёт нагрузок, токов КЗ, селективности и сечений — по проекту ЭОМ организации с допуском СРО; лист задаёт состав, расположение и группы.
8. Ведомость светильников (тип, количество, мощность, поток, Tц, Ra) — лист 64.
9. Оценка освещённости (по норме СанПиН 1.2.3685-21, табл. 5.52, на полу; не светотехнический расчёт, декоративная подсветка в оценку не входит) — лист 40.

1000 мм · печать 1:1

Изм.	Кол.уч	Лист	№ док.	Подп.	Дата
Разраб.		Кырлан А.С.			04.11.26
Пров.					
ГИП					
Н. контр.					
Утв.					

ГД-2026-012-АИ

Дом 120 м²

Общая площадь 147,36* м² · * размеры приняты, не замерены (реестр — л. 7–9, К-1)

Дизайн-проект интерьера

Стадия	Лист	Листов
РП	36	175

План освещения · 1-й этаж

М 1:50


Кырлан Александр Сергеевич

выпуск 04.11.2026 № 4dfa962484 · стр. 37 из 180

План освещения · 2-й этаж

Светильники, группы включения, извещатели · размеры в мм

ПРЕДВАРИТЕЛЬНО · не для производства работ · открыто пунктов: 11 (реестр — л. 7–9)

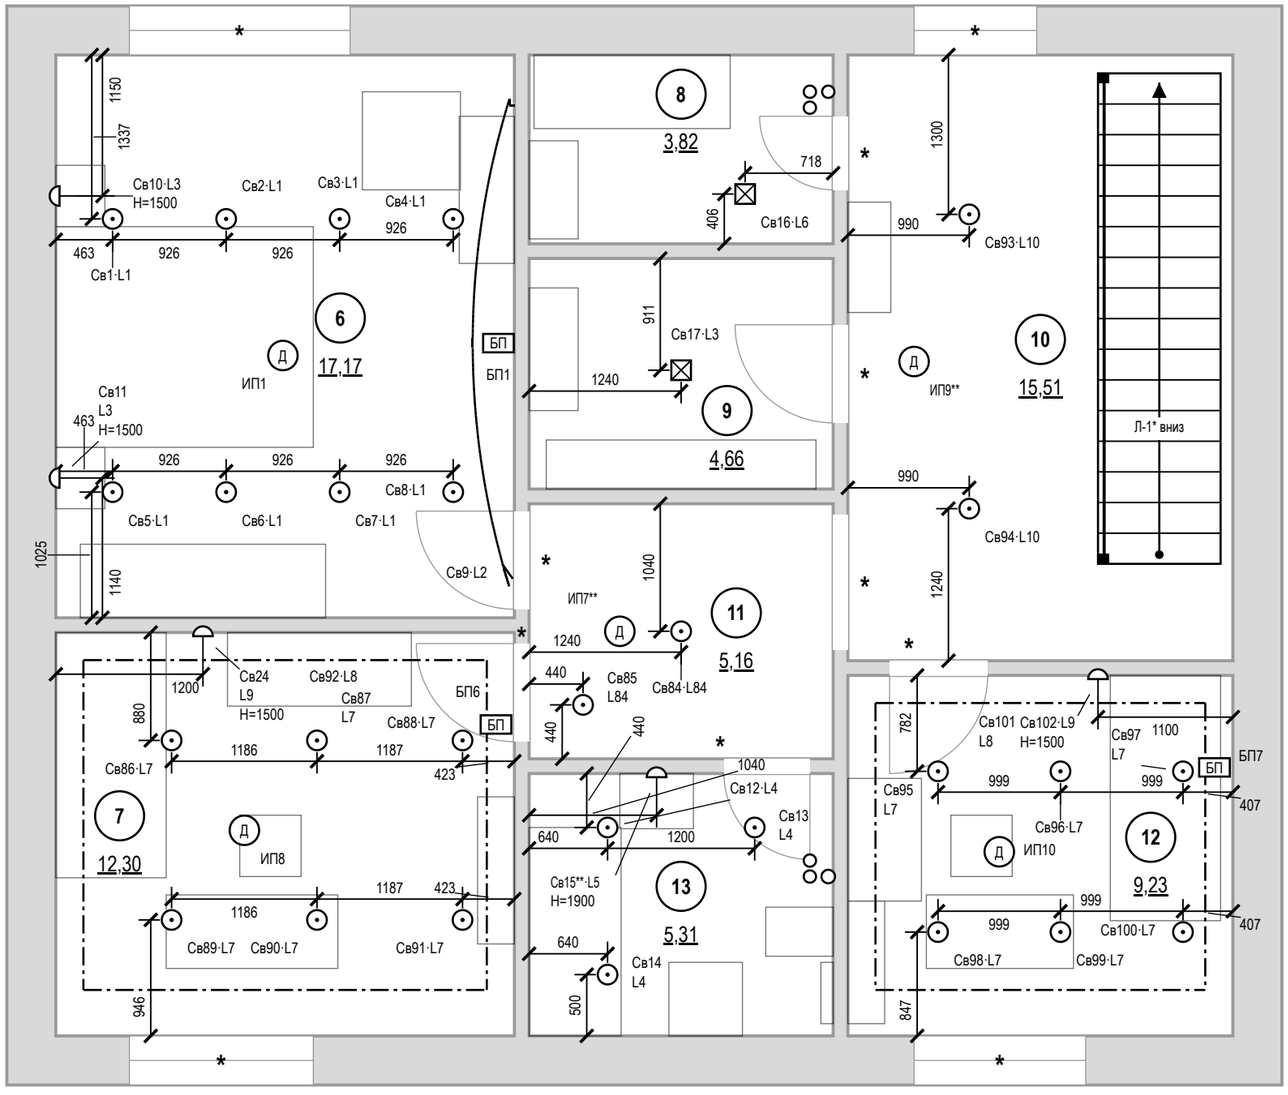

Условные обозначения

- светильник встраиваемый точечный
- светильник потолочный накладной
- светильник настенный (бра), H — высота оси
- светодиодная лента в профиле / в карнизе короба
- Св1·L1 — марка светильника (как в ведомости и на развёртках) · группа включения L (лист 38)
- Д — извещатель пожарный дымовой автономный
- БП — блок питания LED, с доступом (люк от 100×100 мм)
- мебель и сантехприборы — подложка
- стояк: К1 — канализация, В1 — ХВС, Т3 — ГВС
- 1 — номер помещения, площадь м²

Допущения и предложения на листе

Основа листа: взаимное расположение помещений, контур дома 9600 × 8000 и раскладка этажей подобраны проектировщиком под габариты помещений брифа; обмер и проект АР — задание (К-1); высота потолка 2900 мм — по брифу, не замерена; перекрытие 330 мм и отметка 2-го этажа +3,230 приняты; проект КР — задание (К-2); наружные стены 400 мм, перегородки 120 мм приняты (в брифе толщин нет) (К-1); разрешённая мощность 15 кВт принята по типовым ТУ для частного дома (К-4); подрайон климата не задан — принят не северный (жилые от 2,5 м) (К-7).

Знак «*» — принято, не замерено и не подтверждено (замерить на объекте): К-1: окно пом. 6 (стена А), 7 (В), 10 (А), 12 (В) — окно: место, ширина, высота и подоконник приняты по брифу, стена — по раскладке проектировщика (К-1), не замерены; дверь пом. 6 (стена Б), 7 (Б), 8 (Б), 9 (Б), 11 (Б), 12 (А) — проём: место и ширина приняты проектировщиком по брифу (раскладка этажей — К-1), не замерены; дверь пом. 13 (стена А) — Петли у правого откоса (х 6150, у стояков): открытое полотно стоит вдоль стены Б, вошедший идёт влево к умывальнику и ванне; К-2: отметка чистого пола этажа «2-й этаж» +3,230 — отметка чистого пола 2-го этажа +3,230 принята: высота потолка 2900 по брифу + перекрытие с полом 330 (конструкция перекрытия не задана; проект КР — задание); К-3: Л-1 — место, тип и размеры лестницы брифом не заданы (только «лестница из холла 1-го этажа»): одномаршевая 17 × 190 × 250 вдоль стены Б холла — предложение проектировщика; конструкция и расчёт — проект КР; К-5: Ст К1-1, Ст В1-1, Ст Т3-1, Ст К1-2 (кухня), Ст В1-2, Ст Т3-2 — положение стояка принято проектировщиком (проект ВК дома не передан), не замерено.

Знак «**» — предложение проектировщика, заказчиком не утверждено (согласовать с заказчиком): ИП9, ИП7 — дымовой автономный вместо теплового образца: жилой дом — автономные дымовые в путях эвакуации (СП 486, пункт сверить по действующей редакции); ИЗ-1: Св15 — Бра над умывальником См4 — по оси раковины (offset 1100).

См. лист открытых вопросов (лист 7, записи К-1–К-5; лист 8, запись К-7; лист 9, запись ИЗ-1).

Примечания

1. За отметку 0,000 принят уровень чистого пола. Высоты H — от чистого пола до оси изделия; привязки — от чистовой грани стены до оси механизма (у рамки на несколько постов — до оси рамки).
2. Высота установки, не указанная на плане: светильники — на потолке; настенные — по отметке H у знака. Привязки — до оси светильника от чистовой грани стены, по рядам.
3. Во влажных помещениях — светильники не ниже IP44; в зонах 0–2 ванной — по ГОСТ Р 50571.7.701-2024 (зона 1 — IPX5).
4. LED-лента в карнизе подсветки короба — по линии карниза с плана потолков; блок питания — в люке короба (БП на плане), питание ленты длиннее 5 м — с двух концов.
5. Розеточные и мокрые линии — через УЗО или дифавтомат с током утечки не более 30 мА (ПУЭ 7.1.79); в санузле выполнить ДСУП (ПУЭ 7.1.87–7.1.88).
6. Кабель — медный, исполнение нг(А)-LS (ГОСТ 31565-2012); скрытая прокладка только горизонтально и вертикально, фактические трассы зафиксировать исполнительной схемой до закрытия отделкой.
7. Расчёт нагрузок, токов КЗ, селективности и сечений — по проекту ЭОМ организации с допуском СРО; лист задаёт состав, расположение и группы.
8. Ведомость светильников (тип, количество, мощность, поток, Tц, Ra) — лист 64.
9. Оценка освещённости (по норме СанПиН 1.2.3685-21, табл. 5.52, на полу; не светотехнический расчёт, декоративная подсветка в оценку не входит) — лист 40.

1000 мм · печать 1:1

Изм.	Кол.уч	Лист	№ док.	Подп.	Дата
Разраб.		Кырлан А.С.			04.11.26
Пров.					
ГИП					
Н. контр.					
Утв.					

ГД-2026-012-АИ

Дом 120 м²

Общая площадь 147,36* м² · * размеры приняты, не замерены (реестр — л. 7–9, К-1)

Дизайн-проект интерьера

Стадия	Лист	Листов
РП	37	175

План освещения · 2-й этаж

М 1:50


Кырлан Александр Сергеевич

выпуск 04.11.2026 № 4dfa962484 · стр. 38 из 180

План выключателей и схема включения · 1-й этаж

Выключатели S, группы включения L, линии связи · размеры в мм

ПРЕДВАРИТЕЛЬНО · не для производства работ · открыто пунктов: 11 (реестр — л. 7–9)

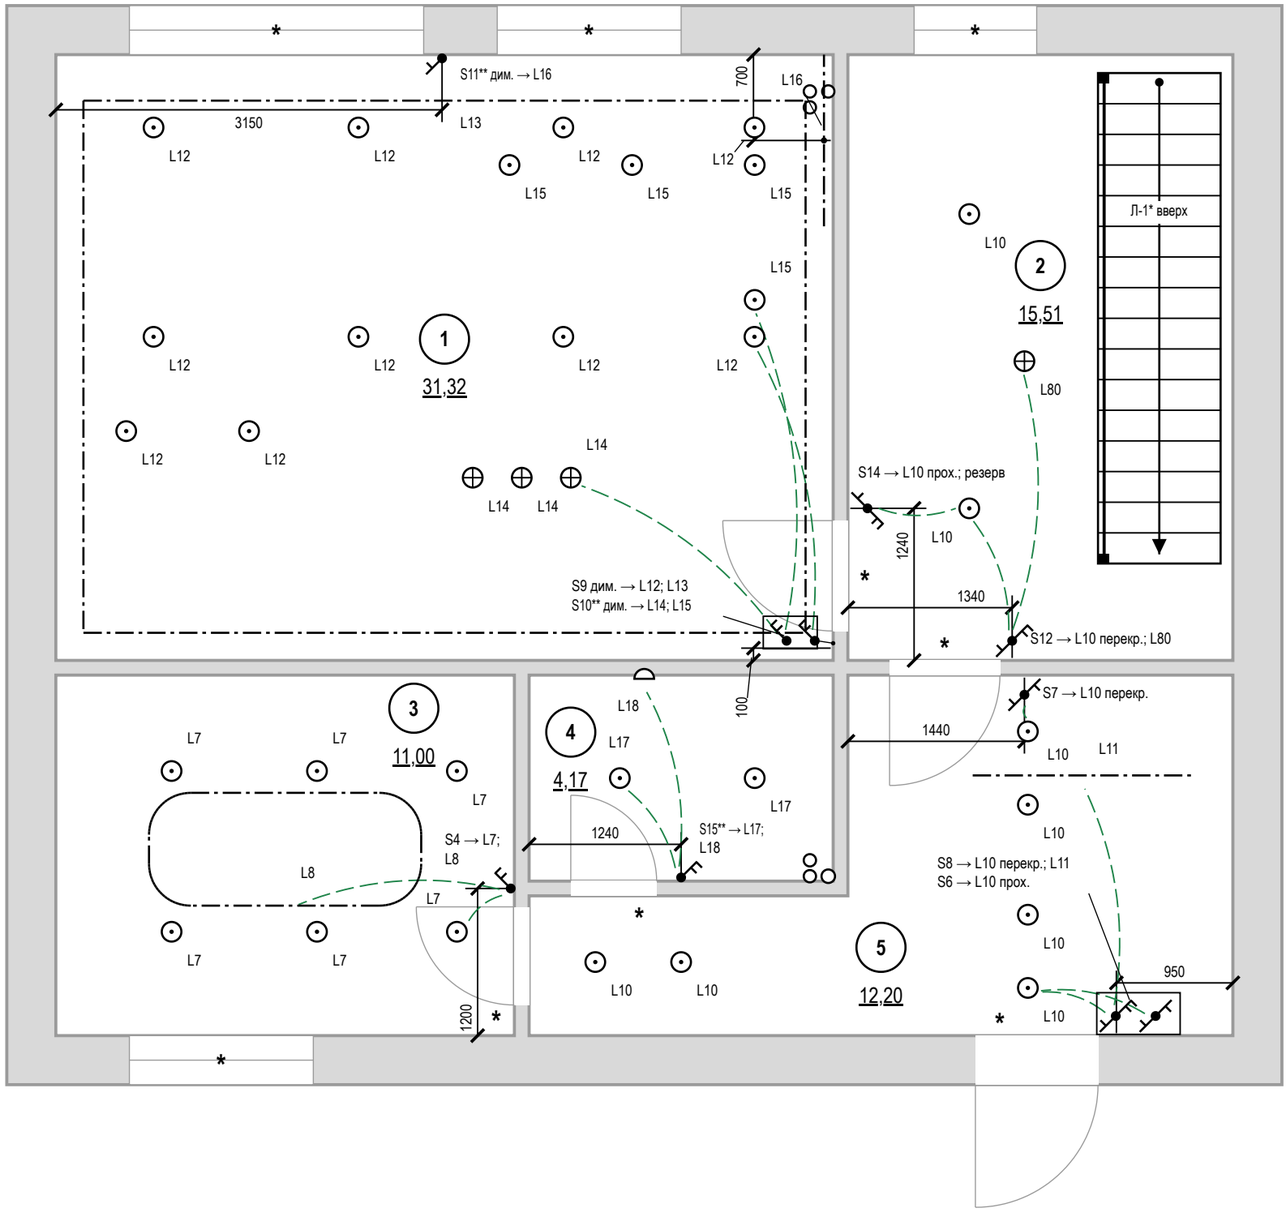

Условные обозначения

- выключатель одноклавишный
- выключатель двухклавишный (флажков — по числу клавиш)
- выключатель с проходной или перекрёстной клавишей (обратный флажок); тип клавиши — в подписи
- S1 → — марка → группы по клавишам (через «;»): прох. — проходной, перекр. — перекрёстный, дим. — светорегулятор; Н — высота
- связь: выключатель → ближайший светильник группы в том же помещении (не трасса кабеля); полный состав группы — по номеру L
- светильник встраиваемый точечный
- светильник подвесной
- светильник настенный (бра), Н — высота оси
- линейный светильник настенный (подсветка столешницы), точка — вывод питания
- светодиодная лента в профиле / в карнизе короба
- L1 — группа включения у светильника
- стояк: К1 — канализация, В1 — ХВС, Т3 — ГВС
- (1) — номер помещения, площадь м²

Допущения и предложения на листе

Основа листа: взаимное расположение помещений, контур дома 9600 × 8000 и раскладка этажей подобраны проектировщиком под габариты помещений брифа; обмер и проект АР — задание (К-1); высота потолка 2900 мм — по брифу, не замерена; перекрытие 330 мм и отметка 2-го этажа +3,230 приняты; проект КР — задание (К-2); наружные стены 400 мм, перегородки 120 мм приняты (в брифе толщин нет) (К-1); разрешённая мощность 15 кВт принята по типовым ТУ для частного дома (К-4); подрайон климата не задан — принят не северный (жилые от 2,5 м) (К-7).

Знак «*» — принято, не замерено и не подтверждено (замерить на объекте): К-1: окно пом. 1 (стена А), 2 (А), 3 (В) — окно: место, ширина, высота и подоконник приняты по брифу, стена — по раскладке проектировщика (К-1), не замерены; дверь пом. 1 (стена Б), 3 (Б), 4 (В), 5 (А) — проём: место и ширина приняты проектировщиком по брифу (раскладка этажей — К-1), не замерены; дверь пом. 5 (стена В) — входная дверь: место и ширина проёма приняты проектировщиком по брифу (без плана дома), не замерены; К-3: Л-1 — место, тип и размеры лестницы брифом не заданы (только «лестница из холла 1-го этажа»): одномаршевая 17 × 190 × 250 вдоль стены Б холла — предложение проектировщика; конструкция и расчёт — проект КР; К-5: Ст К1-1, Ст В1-1, Ст Т3-1, Ст К1-2 (кухня), Ст В1-2, Ст Т3-2 — положение стояка принято проектировщиком (проект ВК дома не передан), не замерено.

Знак «**» — предложение проектировщика, заказчиком не утверждено (согласовать с заказчиком): S10, S11 — светорегулятор добавлен разработчиком проекта; S15 — Сдвиг под раскладку плитки стены В на 50 мм вдоль стены — ось на шве или в центре плитки, привязка по таблице листа.

См. лист открытых вопросов (лист 7, записи К-1–К-5; лист 8, запись К-7).

Примечания

1. За отметку 0,000 принят уровень чистого пола. Высоты Н — от чистого пола до оси изделия; привязки — от чистовой грани стены до оси механизма (у рамки на несколько постов — до оси рамки).
2. Высота установки, не указанная на плане: выключатели — 900 мм от чистого пола (у кровати и другие — Н у марки), со стороны дверной ручки (ПУЭ 7.1.51).
3. Какой выключатель какие светильники включает — по номеру группы L: у выключателя (S1 → L1; L2 — клавиши по порядку) и у каждого светильника. Пунктир подсказка к ближайшему светильнику группы в том же помещении (не дальше 3 м), это не трасса кабеля; выключатель за стеной (у двери санузла) и далёкая группа — только номер группы.
4. Группы из нескольких мест (L10 — S6, S7, S8, S12, S14): на крайних местах — проходные клавиши, на промежуточных — перекрёстные; механизмы — в ведомости изделий.
5. Светорегулятор — по заднему фронту (для LED-драйверов), совместимость с драйверами проверить до закупки.
6. Розеточные и мокрые линии — через УЗО или дифавтомат с током утечки не более 30 мА (ПУЭ 7.1.79); в санузле выполнить ДСУП (ПУЭ 7.1.87–7.1.88).
7. Кабель — медный, исполнение нг(А)-LS (ГОСТ 31565-2012); скрытая прокладка только горизонтально и вертикально, фактические трассы зафиксировать исполнительной схемой до закрытия отделкой.
8. Расчёт нагрузок, токов КЗ, селективности и сечений — по проекту ЭОМ организации с допуском СРО; лист задаёт состав, расположение и группы.
9. Расшифровка клавиш и ведомость изделий — лист 40.

1000 мм · печать 1:1

Изм.	Кол.уч	Лист	№ док.	Подп.	Дата
Разраб.		Кырлан А.С.			04.11.26
Пров.					
ГИП					
Н. контр.					
Утв.					

ГД-2026-012-АИ

Дом 120 м²

Общая площадь 147,36* м² · * размеры приняты, не замерены (реестр — л. 7–9, К-1)

Дизайн-проект интерьера

Стадия	Лист	Листов
РП	38	175

План выключателей и схема включения · 1-й этаж

М 1:50


Кырлан Александр Сергеевич

выпуск 04.11.2026 № 4dfa962484 · стр. 39 из 180

План выключателей и схема включения · 2-й этаж

Выключатели S, группы включения L, линии связи · размеры в мм

ПРЕДВАРИТЕЛЬНО · не для производства работ · открыто пунктов: 11 (реестр — л. 7–9)

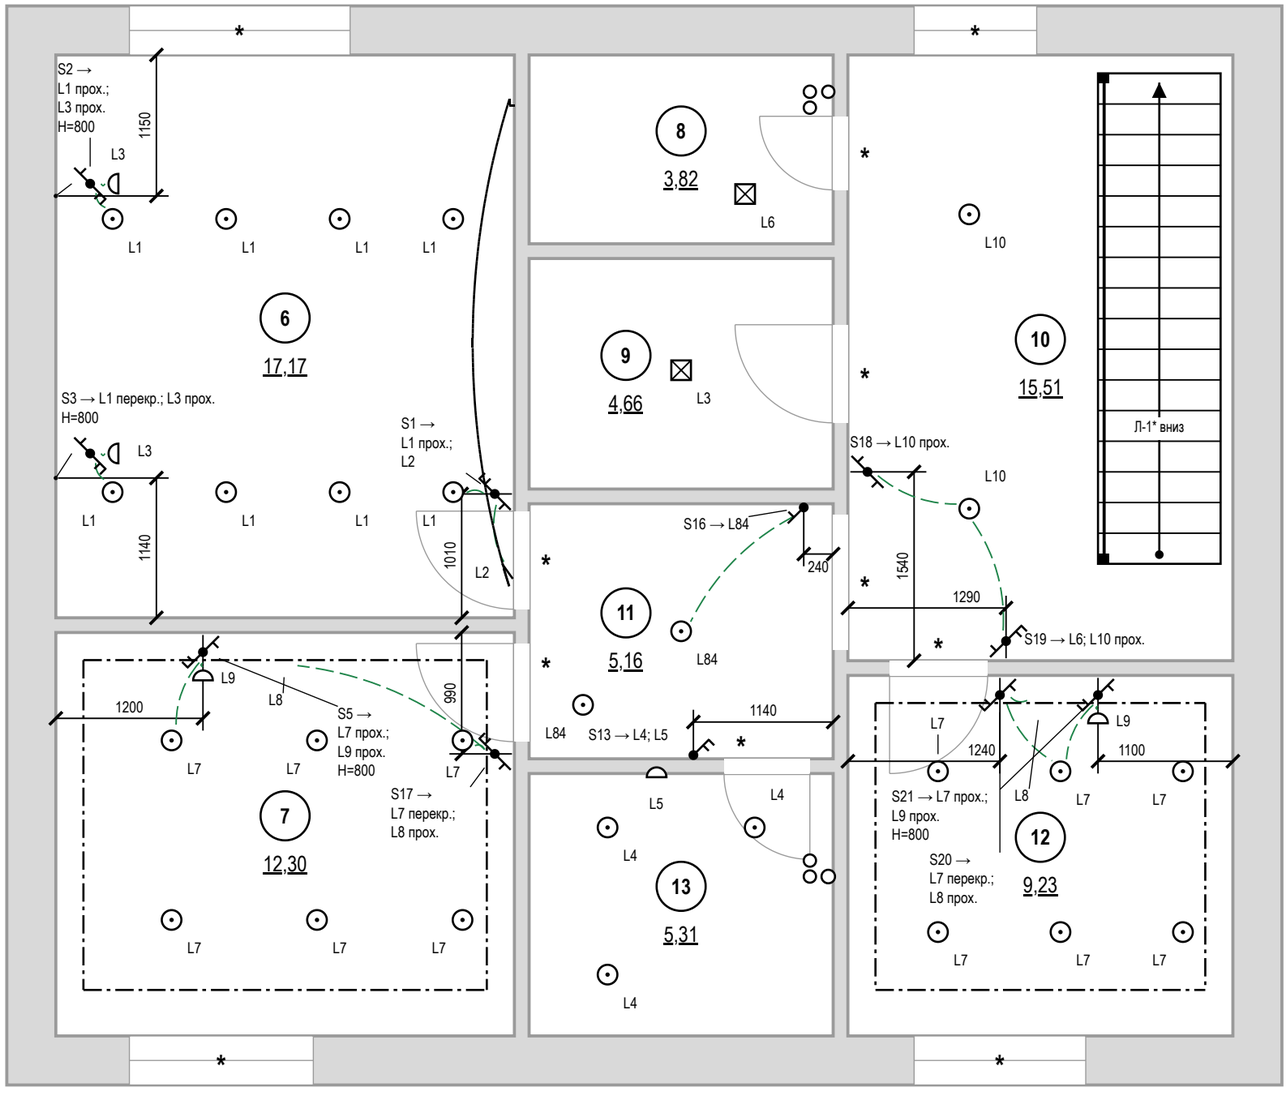

Условные обозначения

- выключатель одноклавишный
- выключатель двухклавишный (флажков — по числу клавиш)
- выключатель с проходной или перекрёстной клавишей (обратный флажок); тип клавиши — в подписи
- S1 → — марка → группы по клавишам (через «;»): прох. — проходной, перекр. — перекрёстный, дим. — светорегулятор; Н — высота
- связь: выключатель → ближайший светильник группы в том же помещении (не трасса кабеля); полный состав группы — по номеру L
- светильник встраиваемый точечный
- светильник потолочный накладной
- светильник настенный (бра), Н — высота оси
- светодиодная лента в профиле / в карнизе короба
- L1 — группа включения у светильника
- стояк: К1 — канализация, В1 — ХВС, Т3 — ГВС
- 1 — номер помещения, площадь м²

Допущения и предложения на листе

Основа листа: взаимное расположение помещений, контур дома 9600 × 8000 и раскладка этажей подобраны проектировщиком под габариты помещений брифа; обмер и проект АР — задание (К-1); высота потолка 2900 мм — по брифу, не замерена; перекрытие 330 мм и отметка 2-го этажа +3,230 приняты; проект КР — задание (К-2); наружные стены 400 мм, перегородки 120 мм приняты (в брифе толщин нет) (К-1); разрешённая мощность 15 кВт принята по типовым ТУ для частного дома (К-4); подрайон климата не задан — принят не северный (жилые от 2,5 м) (К-7).

Знак «*» — принято, не замерено и не подтверждено (замерить на объекте): К-1: окно пом. 6 (стена А), 7 (В), 10 (А), 12 (В) — окно: место, ширина, высота и подоконник приняты по брифу, стена — по раскладке проектировщика (К-1), не замерены; дверь пом. 6 (стена Б), 7 (Б), 8 (Б), 9 (Б), 11 (Б), 12 (А) — проём: место и ширина приняты проектировщиком по брифу (раскладка этажей — К-1), не замерены; дверь пом. 13 (стена А) — Петли у правого откоса (х 6150, у стояков): открытое полотно стоит вдоль стены Б, вошедший идёт влево к умывальнику и ванне; К-2: отметка чистого пола этажа «2-й этаж» +3,230 — отметка чистого пола 2-го этажа +3,230 принята: высота потолка 2900 по брифу + перекрытие с полом 330 (конструкция перекрытия не задана; проект КР — задание); К-3: Л-1 — место, тип и размеры лестницы брифом не заданы (только «лестница из холла 1-го этажа»): одномаршевая 17 × 190 × 250 вдоль стены Б холла — предложение проектировщика; конструкция и расчёт — проект КР; К-5: Ст К1-1, Ст В1-1, Ст Т3-1, Ст К1-2 (кухня), Ст В1-2, Ст Т3-2 — положение стояка принято проектировщиком (проект ВК дома не передан), не замерено.

См. лист открытых вопросов (лист 7, записи К-1–К-5; лист 8, запись К-7).

Примечания

1. За отметку 0,000 принят уровень чистого пола. Высоты Н — от чистого пола до оси изделия; привязки — от чистовой грани стены до оси механизма (у рамки на несколько постов — до оси рамки).
2. Высота установки, не указанная на плане: выключатели — 900 мм от чистого пола (у кровати и другие — Н у марки), со стороны дверной ручки (ПУЭ 7.1.51).
3. Какой выключатель какие светильники включает — по номеру группы L: у выключателя (S1 → L1; L2 — клавиши по порядку) и у каждого светильника. Пунктир подсказка к ближайшему светильнику группы в том же помещении (не дальше 3 м), это не трасса кабеля; выключатель за стеной (у двери санузла) и далёкая группа — только номер группы.
4. Группы из нескольких мест (L1 — S1, S2, S3; L3 — S2, S3; L7 — S5, S17, S20, S21; L8 — S17, S20; L9 — S5, S21; L10 — S18, S19): на крайних местах — проходные клавиши, на промежуточных — перекрёстные; механизмы — в ведомости изделий.
5. Розеточные и мокрые линии — через УЗО или дифавтомат с током утечки не более 30 мА (ПУЭ 7.1.79); в санузле выполнить ДСУП (ПУЭ 7.1.87–7.1.88).
6. Кабель — медный, исполнение нг(А)-LS (ГОСТ 31565-2012); скрытая прокладка только горизонтально и вертикально, фактические трассы зафиксировать исполнительной схемой до закрытия отделкой.
7. Расчёт нагрузок, токов КЗ, селективности и сечений — по проекту ЭОМ организации с допуском СРО; лист задаёт состав, расположение и группы.
8. Расшифровка клавиш и ведомость изделий — лист 40.

1000 мм · печать 1:1

Изм.	Кол.уч	Лист	№ док.	Подп.	Дата
Разраб.		Кырлан А.С.			04.11.26
Пров.					
ГИП					
Н. контр.					
Утв.					

ГД-2026-012-АИ

Дом 120 м²

Общая площадь 147,36* м² · * размеры приняты, не замерены (реестр — л. 7–9, К-1)

Дизайн-проект интерьера

Стадия	Лист	Листов
РП	39	175

План выключателей и схема включения · 2-й этаж

М 1:50

Кырлан Александр Сергеевич

выпуск 04.11.2026 № 4dfa962484 · стр. 40 из 180

02

Электрооборудование

Кырлан Александр Сергеевич

выпуск 04.11.2026 № 4dfa962484 · стр. 41 из 180

Ведомость электроточек и изделий

Электроточки, изделия, светильники, освещённость, клавиши выключателей · б/м

Ведомость электроточек

Марка	Пом.	Назначение	Н, мм	Гр.
Р18**	1	ТВ (в одной зоне с ТВ1, LAN3)	1100	6
Р19**	1	ТВ-приставка (в одной зоне с ТВ1, LAN3)	1100	6
Р20	1	у ТВ-тумбы	300	6
Р21	1	торшер	300	6
Р22	1	у кресла	300	6
Р23	1	уборка, пылесос	300	6
Р24	1	у обеденного стола	300	6
Р25**	1	холодильник Кх9 (розетка в соседнем модуле Кх8, съёмная панель)	150	11
Р26**	1	фартук	1200	7
Р27**	1	фартук	1200	7
Р28**	1	фартук	1175	7
Р29**	1	фартук	1175	7
Р30**	1	фартук между мойкой и варочной	1175	7
Р31**	1	фартук между мойкой и варочной	1175	7
Р32	1	посудомоечная машина	300	10
ЭВ1	1	варочная панель Кх7 (вывод в соседнем модуле Кх6, за ящиком)	600	8
ЭВ2	1	духовой шкаф	150	9
ЭВ3	1	вытяжка	2200	11
Р34	2	уборка	300	6
Р9	3	у стола Кб1** (ноутбук, настольная лампа)	600	5
Р10	3	у стола Кб1** (ноутбук, настольная лампа)	600	5
Р11	3	торшер у кресла Кб4	300	5
Р13	3	уборка	300	5
Р14	3	уборка у входа	300	5
КУП2**	4	КУП — уравнивание потенциалов (ДСУП)	300	
Р33**	4	фен у умывальника, IP44	1000	16
ЭВ5**	4	вентилятор ВР3 (таймер выбега)	2403	3
Р15	5	пылесос, сушилка обуви	300	6
Р16	5	уборка	300	6

Ведомость электроточек (продолжение)

Марка	Пом.	Назначение	Н, мм	Гр.
Р17**	5	питание слаботочного щита (рядом с ЩС**)	1700	17
ЩК	5	щит квартирный ЩРВ-П-48	1700	
Р1	6	у кровати	600	4
Р2	6	у кровати	600	4
Р3	6	рабочий стол	900	4
Р4	6	рабочий стол	900	4
Р5	6	торшер у кресла	300	4
Р6	6	уборка	300	4
Р41	7	у кровати	600	5
Р42	7	у стола Дт2** (настольная лампа, зарядка)	300	5
Р43	7	уборка	300	5
Р44	7	уборка у входа	300	5
Р45	10	уборка	300	6
Р40	11	уборка	300	11
Р46	12	у кровати	600	5
Р47	12	у стола Дт7** (настольная лампа, зарядка)	300	5
Р48	12	уборка	300	5
Р49	12	уборка у входа	300	5
КУП1**	13	КУП — уравнивание потенциалов (ДСУП)	300	
Р7**	13	стиральная машина, IP44	1000	15
Р8**	13	фен у умывальника, IP44	1000	16
ЭВ4**	13	вентилятор ВР1 (таймер выбега)	2403	3
ЭВ6**	13	полотенцесушитель П10, IP44	700	16

Ведомость изделий

Наименование	Марки	Ед.	Кол.
Розетка с з/к и защитными шторками, 16 А	по ведомости точек	шт	45
Розетка IP44 с крышкой, 16 А	Р7**, Р8**, Р33**	шт	3
Выключатель 1-клав.	S16	шт	1
Выключатель 1-клав. перекрёстный	S7	шт	1
Выключатель 1-клав. проходной	S6, S18	шт	2

Ведомость изделий (продолжение)

Наименование	Марки	Ед.	Кол.
Выключатель 2-клав.	S13, S15**	шт	2
Выключатель 2-клав. (перекрёстная + обычная)	S8, S12	шт	2
Выключатель 2-клав. (перекрёстная + проходная)	S3, S4, S14, S19, S20	шт	5
Выключатель 2-клав. (проходная + обычная)	S1	шт	1
Выключатель 2-клав. перекрёстный	S17	шт	1
Выключатель 2-клав. проходной	S2, S5, S21	шт	3
Светорегулятор 1-канальный, задний фронт (LED)	S11**	шт	1
Светорегулятор 2-канальный, задний фронт (LED)	S9, S10**	шт	2
Датчик движения ночной подсветки	L11	шт	1
Рамка 1-постовая	в т. ч. 21 под выключ.	шт	59
Рамка 2-постовая		шт	5
Коробка установочная (подрозетник) Ø68	розетки, выключатели	шт	69
Вывод кабеля под прибор (клеммник)	ЭВ1–ЭВ3, ЭВ4**, ЭВ5**, ЭВ6**	шт	6
Коробка уравнивания потенциалов КУП	КУП1**, КУП2**	шт	2
Блок питания LED 24 В, 300 Вт, дим.	БП4	шт	1
Блок питания LED 24 В, 60 Вт, дим.	БП5**	шт	1
Блок питания LED 24 В, 200 Вт, дим.	БП1, БП2, БП6, БП7	шт	4
Блок питания LED 24 В, 20 Вт	БП3	шт	1
Извещатель дымовой автономный	ИП1, ИП2, ИП3**, ИП4, ИП6**, ИП7**, ИП8, ИП9**, ИП10	шт	9
Извещатель тепловой	ИП5	шт	1
Щит квартирный (состав — лист щита)	ЩК	шт	1
Розетка компьютерная RJ45, кат. 6, с рамкой и подрозетником	LAN2–LAN5	шт	4
Розетка телевизионная (коаксиальная) с рамкой и подрозетником	ТВ1	шт	1
Точка доступа Wi-Fi (оборудование заказчика), питание PoE	АР1**, АР2**	шт	2
Трубка или монитор домофона (поставка домофонной организации)	ДФ1	шт	1

Ведомость изделий (продолжение)

Наименование	Марки	Ед.	Кол.
Щит слаботочный ЩС**: корпус, DIN-рейка, розетки 220 В	ЩС**	шт	1
Патч-панель, портов не менее 6		шт	1
Коммутатор, портов не менее 6, из них PoE 2		шт	1
Кабель домофона — тип по системе поставщика (по лучам от ЩС**, запас 10 %)		м	6,1
Кабель коаксиальный RG-6 (75 Ом) к розеткам ТВ (по лучам от ЩС**, запас 10 %)		м	16,7
Кабель U/UTP кат. 6 (LAN, Wi-Fi и камеры по PoE) (по лучам от ЩС**, запас 10 %)		м	71

Ведомость светильников

Поз.	Марки	Тип	Кол.	Р, Вт	Ф, лм	IP	Тц/Ra
1	Св31–Св40	встраиваемый точечный	10	12	1000		3000/90
2	Св41	светодиодная лента, 20,5 м	1	196,8	18450		2700/90
3	Св42**, Св43**, Св44**	подвесной	3	9	800		3000/90
4	Св45–Св48	встраиваемый точечный	4	10	900		3000/90
5	Св49**	линейный светильник, Н=1440	1	18	1500		3000/90
6	Св26–Св29, Св53, Св54, Св82–Св85, Св93, Св94	встраиваемый точечный	12	7	600		3000/90
7	Св80	подвесной	1	12	1100		3000/90
8	Св17–Св22	встраиваемый точечный	6	14	1400		2700/90
9	Св23	светодиодная лента, 5,7 м	1	54,7	5130		2700/90
10	Св50	встраиваемый точечный	1	7	600	44	3000/90
11	Св12–Св14, Св51	встраиваемый точечный	4	6	500	44	3000/90
12	Св15**, Св52**	настенный (бра), Н=1900	2	8	600	44	3000/90
13	Св30**	светодиодная лента, 1,8 м	1	8,6	270		2700/90
14	Св1–Св8	встраиваемый точечный	8	12	1000		2700/90

Примечания

1. Ведомости сведены с планов розеток, освещения и выключателей; марки, группы и высоты — те же, что у знаков на планах.
2. Механизмы, рамки и светорегуляторы — одной серии; число постов и клавиш сверено с выбранной серией. Перекрёстная клавиша — отдельный механизм серии.
3. Освещённость (оценка) — по норме СанПиН 1.2.3685-21 (табл. 5.52, на полу), не светотехнический расчёт; декоративная подсветка в оценку не входит.
4. За отметку 0,000 принят уровень чистого пола. Высоты Н — от чистого пола до оси изделия; привязки — от чистовой грани стены до оси механизма (у рамки на несколько постов — до оси рамки).
5. Розеточные и мокрые линии — через УЗО или дифавтомат с током утечки не более 30 мА (ПУЭ 7.1.79); в санузле выполнить ДСУП (ПУЭ 7.1.87–7.1.88).
6. Кабель — медный, исполнение нг(А)-LS (ГОСТ 31565-2012); скрытая прокладка только горизонтально и вертикально, фактические трассы зафиксировать исполнительной схемой до закрытия отделкой.
7. Расчёт нагрузок, токов КЗ, селективности и сечений — по проекту ЭОМ организации с допуском СРО; лист задаёт состав, расположение и группы.
8. Ведомости занимают 2 листов этого наименования: таблицы, не вошедшие в поле листа, продолжены на следующем листе.

Допущения и предложения на листе. Знак «**» предложено (согласовать). См. лист открытых вопросов (листы 7–9).

Изм.	Кол.уч	Лист	№ док.	Подп.	Дата
Разраб.		Кырлан А.С.			04.11.26
Пров.					
ГИП					
Н. контр.					
Утв.					

ГД-2026-012-АИ

Дом 120 м²

Общая площадь 147,36* м² · * размеры приняты, не замерены (реестр — л. 7–9, К-1)

Дизайн-проект интерьера

Стадия	Лист	Листов
РП	40	175

Ведомость электроточек и изделий

М б/м

Кырлан Александр Сергеевич

выпуск 04.11.2026 № 4dfa962484 · стр. 42 из 180

Ведомость электроточек и изделий (продолжение)

Электроточки, изделия, светильники, освещённость, клавиши выключателей · б/м

Ведомость светильников (продолжение)

Поз.	Марки	Тип	Кол.	P, Вт	Ф, лм	IP	Тц/Ra
15	Св9	светодиодная лента, 4,5 м	1	43,2	4050		2700/90
16	Св10, Св11, Св24, Св102	настенный (бра), H=1500	4	6	400		2700/90
17	Св86–Св91, Св95–Св100	встраиваемый точечный	12	11	1100		2700/90
18	Св92	светодиодная лента, 12 м	1	115,2	10800		2700/90
19	Св16	потолочный накладной	1	10	900		3000/90
20	Св25	потолочный накладной	1	9	600		3000/90
21	Св101	светодиодная лента, 10,1 м	1	97	9090		2700/90

Освещённость (оценка)

Пом.	S, м²	Eн, лк	Ф треб., лм	Ф по пр., лм
1	31,3	150	13230	16000
2	15,5	50	2180	2300
3	11	300	9300	8400
4	4,2	50	590	1100
5	12,2	50	1720	3600
6	17,2	150	7250	8000
7	12,3	200	6930	6600
8	3,8	75	810	900
9	4,7	30	390	600
10	15,5	50	2180	1200
11	5,2	50	730	1200
12	9,2	200	5200	6600
13	5,3	50	750	1500

Расшифровка клавиш

Марка	Пом.	H, мм	Клав.	Механизм	Группа: светильники
S1	6	900	1	проходной	L1: Св1–Св8
			2	обычный	L2: Св9
S2	6	800	1	проходной	L1: Св1–Св8
			2	проходной	L3: Св10, Св11, Св25

Расшифровка клавиш (продолжение)

Марка	Пом.	H, мм	Клав.	Механизм	Группа: светильники
S3	6	800	1	перекрёстный	L1: Св1–Св8
			2	проходной	L3: Св10, Св11, Св25
S4	3	900	1	перекрёстный	L7: Св17–Св22, Св86–Св91, Св95–Св100
			2	проходной	L8: Св23, Св92, Св101
S5	7	800	1	проходной	L7: Св17–Св22, Св86–Св91, Св95–Св100
			2	проходной	L9: Св24, Св102
S6	5	900	1	проходной	L10: Св26–Св29, Св53, Св54, Св82, Св83, Св93, Св94
S7	5	900	1	перекрёстный	L10: Св26–Св29, Св53, Св54, Св82, Св83, Св93, Св94
S8	5	900	1	перекрёстный	L10: Св26–Св29, Св53, Св54, Св82, Св83, Св93, Св94
			2	обычный	L11: Св30**
S9	1	900	1	светорегулятор	L12: Св31–Св40
			2	светорегулятор	L13: Св41
S10**	1	900	1	светорегулятор	L14: Св42**, Св43**, Св44**
			2	светорегулятор	L15: Св45–Св48
S11**	1	900	1	светорегулятор	L16: Св49**
S12	2	900	1	перекрёстный	L10: Св26–Св29, Св53, Св54, Св82, Св83, Св93, Св94
			2	обычный	L80: Св80
S13	11	900	1	обычный	L4: Св12–Св14
			2	обычный	L5: Св15**
S14	2	900	1	проходной	L6: Св16
			2	перекрёстный	L10: Св26–Св29, Св53, Св54, Св82, Св83, Св93, Св94
S15**	4	900	1	обычный	L17: Св50, Св51
			2	обычный	L18: Св52**
S16	11	900	1	обычный	L84: Св84, Св85

Расшифровка клавиш (продолжение)

Марка	Пом.	H, мм	Клав.	Механизм	Группа: светильники
S17	7	900	1	перекрёстный	L7: Св17–Св22, Св86–Св91, Св95–Св100
			2	перекрёстный	L8: Св23, Св92, Св101
S18	10	900	1	проходной	L10: Св26–Св29, Св53, Св54, Св82, Св83, Св93, Св94
S19	10	900	1	проходной	L6: Св16
			2	перекрёстный	L10: Св26–Св29, Св53, Св54, Св82, Св83, Св93, Св94
S20	12	900	1	перекрёстный	L7: Св17–Св22, Св86–Св91, Св95–Св100
			2	проходной	L8: Св23, Св92, Св101
S21	12	800	1	проходной	L7: Св17–Св22, Св86–Св91, Св95–Св100
			2	проходной	L9: Св24, Св102

Допущения и предложения на листе

Основа листа: взаимное расположение помещений, контур дома 9600 × 8000 и раскладка этажей подобраны проектировщиком под габариты помещений брифа; обмер и проект АР — задание (К-1); высота потолка 2900 мм — по брифу, не замерена; перекрытие 330 мм и отметка 2-го этажа +3,230 приняты; проект КР — задание (К-2); наружные стены 400 мм, перегородки 120 мм приняты (в брифе толщин нет) (К-1); разрешённая мощность 15 кВт принята по типовым ТУ для частного дома (К-4); подрайон климата не задан — принят не северный (жилые от 2,5 м) (К-7). Знак «**» — предложение проектировщика, заказчиком не утверждено (согласовать с заказчиком): S10, S11 — светорегулятор добавлен разработчиком проекта; Св42, Св43, Св44, Св49 — диммируемость добавлена разработчиком проекта под светорегуляторы S10 и S11; Св52 — Сдвиг под раскладку плитки стены А на 49 мм вдоль стены — ось на шве или в центре плитки, привязка по таблице листа; S15 — Сдвиг под раскладку плитки стены В на 50 мм вдоль стены — ось на шве или в центре плитки, привязка по таблице листа; Св30 — открытая лента в накладном профиле вместо «в коробе»: короба в потолке нет — подвесной потолок помещения без короба и ниши LED; ИЗ-1: Св15 — Бра над умывальником См4 — по оси раковины (offset 1100).

См. лист открытых вопросов (лист 7, записи К-1, К-2, К-4; лист 8, запись К-7; лист 9, запись ИЗ-1).

Примечания

1. Продолжение ведомостей: лист 2 из 2 этого наименования; таблицы, прерванные на предыдущем листе, продолжены с заголовком «(продолжение)».
2. За отметку 0,000 принят уровень чистого пола. Высоты H — от чистого пола до оси изделия; привязки — от чистовой грани стены до оси механизма (у рамки на несколько постов — до оси рамки).
3. Розеточные и мокрые линии — через УЗО или дифавтомат с током утечки не более 30 мА (ПУЭ 7.1.79); в санузле выполнить ДСУП (ПУЭ 7.1.87–7.1.88).
4. Кабель — медный, исполнение нг(А)-LS (ГОСТ 31565-2012); скрытая прокладка только горизонтально и вертикально, фактические трассы зафиксировать исполнительной схемой до закрытия отделкой.
5. Расчёт нагрузок, токов КЗ, селективности и сечений — по проекту ЭОМ организации с допуском СРО; лист задаёт состав, расположение и группы.

Изм.	Кол.уч	Лист	№ док.	Подп.	Дата
Разраб.		Кырлан А.С.			04.11.26
Пров.					
ГИП					
Н. контр.					
Утв.					

ГД-2026-012-АИ

Дом 120 м²

Общая площадь 147,36* м² · * размеры приняты, не замерены (реестр — л. 7–9, К-1)

Дизайн-проект интерьера

Стадия	Лист	Листов
РП	41	175

Ведомость электроточек и изделий (продолжение)


М б/м

Кырлан Александр Сергеевич

выпуск 04.11.2026 № 4dfa962484 · стр. 43 из 180

Однолинейная схема щита

Щит квартирный ЩК · гр. 1—9 из 17 · без масштаба

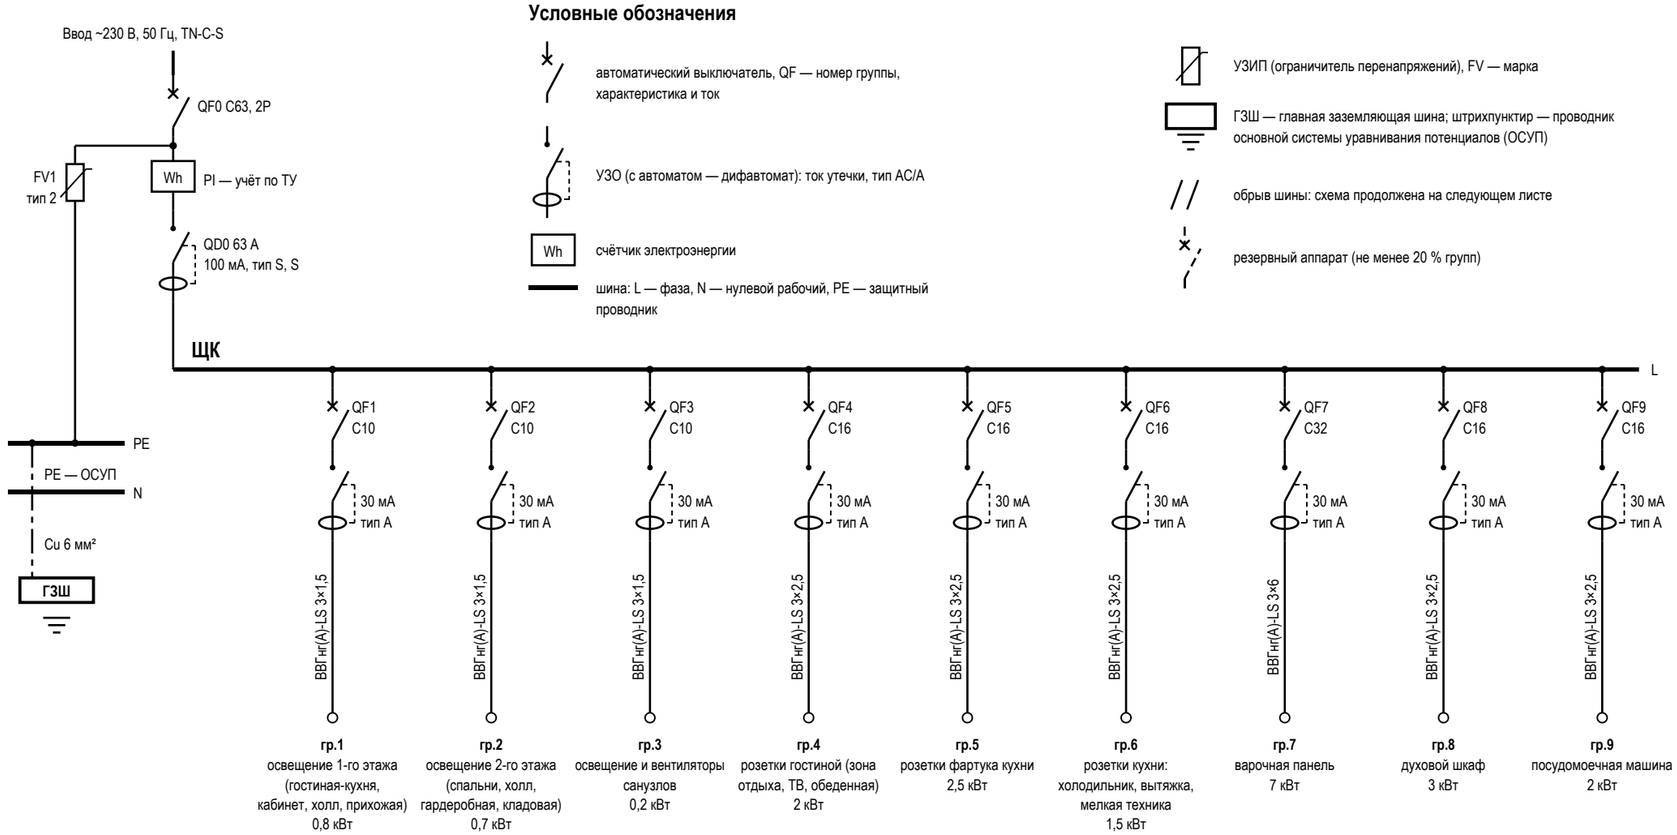

Условные обозначения

- автоматический выключатель, QF — номер группы, характеристика и ток
- УЗО (с автоматом — дифавтомат): ток утечки, тип AC/A
- Wh — счётчик электроэнергии
- шина: L — фаза, N — нулевой рабочий, PE — защитный проводник
- УЗИП (ограничитель перенапряжений), FV — марка
- ГЗШ — главная заземляющая шина; штрихпунктир — проводник основной системы уравнивания потенциалов (ОСУП)
- обрыв шины: схема продолжена на следующем листе
- резервный аппарат (не менее 20 % групп)

Данные щитка

Показатель	Значение
Номер щитка	ЩК
Тип	ЩРВ-П-54, IP41
Уст. мощность, кВт	30,4
Разреш. мощность, кВт	15
Расчётная, кВт	12,6
Автоматы 1п: занят. / рез.	17 / 4
Модулей: всего / занято	54 / 40
Ток на вводе, А	63
Вводной аппарат	QF0 C63, 2P
УЗИП	FV1, тип 2, ЩК, после счётчика
ГЗШ, проводник ОСУП	Cu 6 мм²
Листов схемы	2 (группы по листам)

Таблица групп щита ЩК и кабельный журнал

№	Назначение	Помещения	Автомат	УЗО / дифавтомат	Кабель	Длина, м	Р, кВт	Точек
1	освещение 1-го этажа (гостиная-кухня, кабинет, холл, прихожая)	2, 3, 5, 6, 7, 8, 9, 10, 12	C10	30 мА, тип A	ВВГнг(A)-LS 3×1,5	200,9	0,8	53
2	освещение 2-го этажа (спальни, холл, гардеробная, кладовая)	1, 2, 5, 10, 11	C10	30 мА, тип A	ВВГнг(A)-LS 3×1,5	119,3	0,7	42
3	освещение и вентиляторы санузлов	4, 11, 13	C10	30 мА, тип A	ВВГнг(A)-LS 3×1,5	50,6	0,2	11
4	розетки гостиной (зона отдыха, ТВ, обеденная)	6	C16	30 мА, тип A	ВВГнг(A)-LS 3×2,5	37,8	2	6
5	розетки фартука кухни	3, 7, 12	C16	30 мА, тип A	ВВГнг(A)-LS 3×2,5	76,1	2,5	13
6	розетки кухни: холодильник, вытяжка, мелкая техника	1, 2, 5, 10	C16	30 мА, тип A	ВВГнг(A)-LS 3×2,5	60,7	1,5	11
7	варочная панель	1	C32	30 мА, тип A	ВВГнг(A)-LS 3×6	29,8	7	6
8	духовой шкаф	1	C16	30 мА, тип A	ВВГнг(A)-LS 3×2,5	13,9	3	1
9	посудомоечная машина	1	C16	30 мА, тип A	ВВГнг(A)-LS 3×2,5	12,1	2	1

Примечания

1. Схема однолинейная: одна линия — фаза, N и PE группы; аппараты — в отключённом положении (ГОСТ 2.702, ГОСТ 2.755). Номера групп — как у точек на планах (гр.). За отметку 0,000 принят уровень чистого пола; высота щита — по плану розеток.
2. Розеточные и мокрые линии — через УЗО или дифавтомат с током утечки не более 30 мА (ПУЭ 7.1.79); в санузле выполнить ДСУП (ПУЭ 7.1.87–7.1.88).
3. УЗО тип A — для линий с электроникой, стиральной и посудомоечной машиной, LED-драйверами; тип AC — только для чисто активной нагрузки.
4. Кабель — медный, исполнение нг(A)-LS (ГОСТ 31565-2012); скрытая прокладка только горизонтально и вертикально, фактические трассы зафиксировать исполнительной схемой до закрытия отделкой.
5. Номинал автомата — не выше допустимого тока кабеля: 1,5 мм² — до 10 А, 2,5 мм² — до 16 А. Резерв щита — не менее 20 % модулей.
6. Расчёт нагрузок, токов КЗ, селективности и сечений — по проекту ЭОМ организации с допуском СРО; лист задаёт состав, расположение и группы.
7. УЗИП FV1 — после вводного автомата, проводник к шине PE — кратчайший, без петель. Шина PE щита соединяется с ГЗШ проводником ОСУП; к ГЗШ присоединяются трубы водопровода и отопления на вводе в квартиру (ПУЭ 7.1.87). Шины N и PE — раздельные, после разделения PEN не объединяются.
8. До подключения нагрузки — приёмо-сдаточные испытания с протоколом: сопротивление изоляции линий не менее 0,5 МОм, срабатывание УЗО по току и времени, непрерывность защитных проводников PE (ПУЭ, гл. 1.8).

Допущения и предложения на листе

Основа листа: взаимное расположение помещений, контур дома 9600 × 8000 и раскладка этажей подобраны проектировщиком под габариты помещений брифа; обмер и проект АР — задание (К-1); высота потолка 2900 мм — по брифу, не замерена; перекрытие 330 мм и отметка 2-го этажа +3,230 приняты; проект КР — задание (К-2); наружные стены 400 мм, перегородки 120 мм приняты (в брифе толщин нет) (К-1); разрешённая мощность 15 кВт принята по типовым ТУ для частного дома (К-4); подрайон климата не задан — принят не северный (жилые от 2,5 м) (К-7).

Открытые вопросы и конфликты по листу: К-4.

См. лист открытых вопросов (лист 7, записи К-1, К-2, К-4; лист 8, запись К-7).

Изм.	Кол.уч	Лист	№ док.	Подп.	Дата
Разраб.		Кырлан А.С.			04.11.26
Пров.					
ГИП					
Н. контр.					
Утв.					

ГД-2026-012-АИ

Дом 120 м²

Общая площадь 147,36* м² · * размеры приняты, не замерены (реестр — л. 7–9, К-1)

Дизайн-проект интерьера

Стадия	Лист	Листов
РП	42	175

Однолинейная схема щита

М б/м

Кырлан Александр Сергеевич

выпуск 04.11.2026 № 4dfa962484 · стр. 44 из 180

Однолинейная схема щита (продолжение)

Щит квартирный ЩК · гр. 10—17 из 17 · без масштаба

Продолжение однолинейной схемы щита ЩК, начало — лист 42

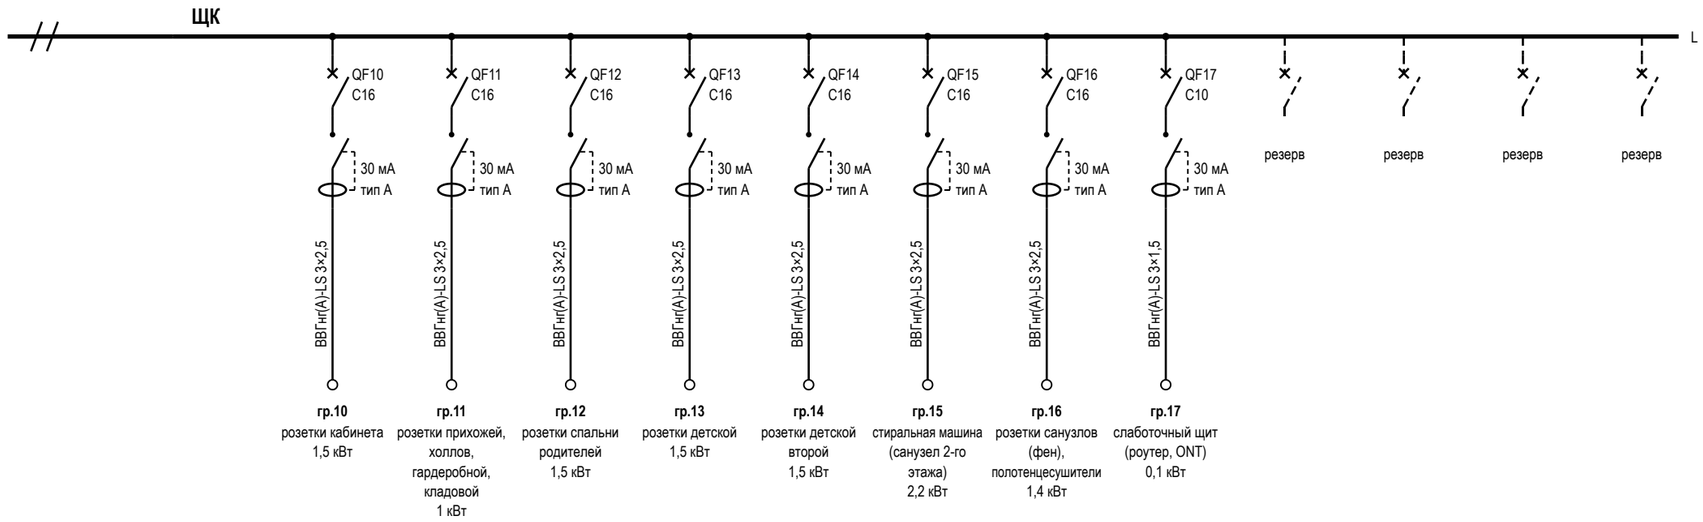


Таблица групп щита ЩК и кабельный журнал (продолжение)

№	Назначение	Помещения	Автомат	УЗО / дифавтомат	Кабель	Длина, м	Р, кВт	Точек
10	розетки кабинета	1	C16	30 мА, тип A	ВВГнг(A)-LS 3×2,5	15,3	1,5	1
11	розетки прихожей, холлов, гардеробной, кладовой	1, 11	C16	30 мА, тип A	ВВГнг(A)-LS 3×2,5	20,9	1	3
12	розетки спальни родителей		C16	30 мА, тип A	ВВГнг(A)-LS 3×2,5	13,8	1,5	0
13	розетки детской		C16	30 мА, тип A	ВВГнг(A)-LS 3×2,5	27,4	1,5	0
14	розетки детской второй		C16	30 мА, тип A	ВВГнг(A)-LS 3×2,5	4,1	1,5	0
15	стиральная машина (санузел 2-го этажа)	13	C16	30 мА, тип A	ВВГнг(A)-LS 3×2,5	20	2,2	1
16	розетки санузлов (фен), полотенцесушители	4, 13	C16	30 мА, тип A	ВВГнг(A)-LS 3×2,5	35	1,4	3
17	слаботочный щит (роутер, ONT)	5	C10	30 мА, тип A	ВВГнг(A)-LS 3×1,5	5	0,1	1
	Итого по сечениям ВВГнг(A)-LS (все группы щита), м: 3×1,5 — 375,8; 3×2,5 — 337,1; 3×6 — 29,8					742,7		

Примечания

1. Лист — продолжение однолинейной схемы щита ЩК: начало, данные щитка и условные обозначения — лист 42. Ввод, учёт, вводной аппарат, УЗИП, шины N и PE и ГЗШ показаны там же; шина L листа — та же шина щита.
2. Схема однолинейная: одна линия — фаза, N и PE группы; аппараты — в отключённом положении (ГОСТ 2.702, ГОСТ 2.755). Номера групп — как у точек на планах (гр.). За отметку 0,000 принят уровень чистого пола; высота щита — по плану розеток.
3. Розеточные и мокрые линии — через УЗО или дифавтомат с током утечки не более 30 мА (ПУЭ 7.1.79); в санузле выполнить ДСУП (ПУЭ 7.1.87–7.1.88).
4. УЗО тип A — для линий с электроникой, стиральной и посудомоечной машиной, LED-драйверами; тип AC — только для чисто активной нагрузки.
5. Кабель — медный, исполнение нг(A)-LS (ГОСТ 31565-2012); скрытая прокладка только горизонтально и вертикально, фактические трассы зафиксировать исполнительной схемой до закрытия отделкой.
6. Номинал автомата — не выше допустимого тока кабеля: 1,5 мм² — до 10 А, 2,5 мм² — до 16 А. Резерв щита — не менее 20 % модулей.
7. Расчёт нагрузок, токов КЗ, селективности и сечений — по проекту ЭОМ организации с допуском СРО; лист задаёт состав, расположение и группы.
8. До подключения нагрузки — приёмо-сдаточные испытания с протоколом: сопротивление изоляции линий не менее 0,5 МОм, срабатывание УЗО по току и времени, непрерывность защитных проводников PE (ПУЭ, гл. 1.8).

Допущения и предложения на листе

Основа листа: взаимное расположение помещений, контур дома 9600 × 8000 и раскладка этажей подобраны проектировщиком под габариты помещений брифа; обмер и проект АР — задание (К-1); высота потолка 2900 мм — по брифу, не замерена; перекрытие 330 мм и отметка 2-го этажа +3,230 приняты; проект КР — задание (К-2); наружные стены 400 мм, перегородки 120 мм приняты (в брифе толщин нет) (К-1); разрешённая мощность 15 кВт принята по типовым ТУ для частного дома (К-4); подрайон климата не задан — принят не северный (жилые от 2,5 м) (К-7).

См. лист открытых вопросов (лист 7, записи К-1, К-2, К-4; лист 8, запись К-7).

Изм.	Кол.уч	Лист	№ док.	Подп.	Дата
Разраб.		Кырлан А.С.			04.11.26
Пров.					
ГИП					
Н. контр.					
Утв.					

ГД-2026-012-АИ

Дом 120 м²


Общая площадь 147,36* м² · * размеры приняты, не замерены (реестр — л. 7–9, К-1)

Дизайн-проект интерьера	Стадия	Лист	Листов
	РП	43	175
Однолинейная схема щита (продолжение) М б/м	**Кырлан Александр Сергеевич**		

План принципиальных трасс · 1-й этаж

Силовые трассы и объёмы электромонтажа, слаботочка в объёмах · размеры в мм

ПРЕДВАРИТЕЛЬНО · не для производства работ · открыто пунктов: 11 (реестр — л. 7–9)

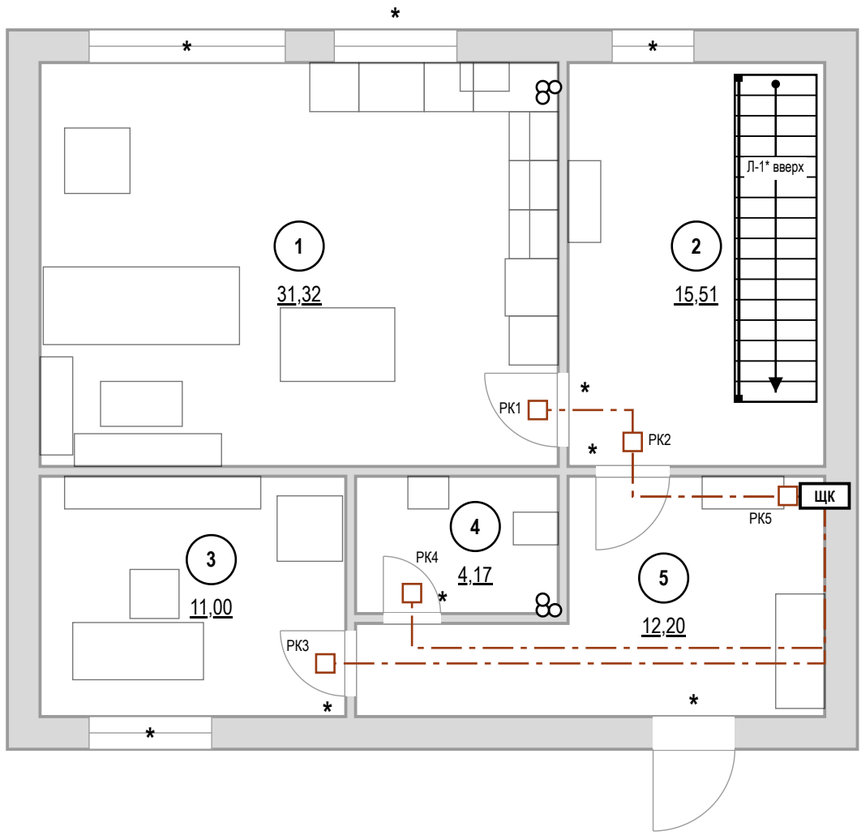

Кабель по группам ВВГнг(А)-LS, м

Гр.	мм²	Трасса	Данные
1	3×1,5	44,2	200,9
2	3×1,5	92,1	119,3
3	3×1,5	22,8	50,6
5	3×2,5	28,1	76,1
6	3×2,5	50,7	60,7
7	3×6	30,8	29,8

Гр.	мм²	Трасса	Данные
8	3×2,5	13,9	13,9
9	3×2,5	12,1	12,1
10	3×2,5	15,3	15,3
11	3×2,5	15,8	20,9
16	3×2,5	17,7	35
17	3×1,5	4,1	5
Σ		**347,6**	**742,7**

Экспликация помещений

№	Помещение	Площадь, м²
1	Гостиная-кухня	31,32
2	Холл с лестницей	15,51
3	Кабинет	11,00
4	Санузел гостевой	4,17
5	Прихожая	12,20
	Итого по этажу	74,20
	Итого по дому	147,36

Объёмы прокладки

Работа, материал	Ед.	Кол.
Гофротруба Ø20 в потолочном пространстве	м	133,6
Кабель-канал плинтуса для силовых линий	м	86,1
Короб или накладной канал для вертикальных спусков и подъёмов	м	65,5
Коробка распределительная (РК) над дверью помещения	шт	5
Слаботочка: кабель домофона	м	6,1
Слаботочка: Кабель коаксиальный RG-6 (75 Ом) к розеткам ТВ	м	16,7
Слаботочка: U/UTP кат. 6 (LAN, Wi-Fi, камеры)	м	47,9
Слаботочка: гофротруба Ø20 отдельно от силовых	м	63,6

Штробы — только после заключения

Работа	Ед.	Кол.
Вертикальные штробы 20×20 мм от потолка до каждой настенной точки (в маршрут без штроб не входят)	м	81,89

Условные обозначения

- **ЩК** — щит квартирный
- РК — распределительная коробка над дверью помещения
- магистраль от щита к РК: потолочное пространство, гофра
- мебель и сантехприборы — подложка

Допущения и предложения на листе

Основа листа: взаимное расположение помещений, контур дома 9600 × 8000 и раскладка этажей подобраны проектировщиком под габариты помещений брифа; обмер и проект АР — задание (К-1); высота потолка 2900 мм — по брифу, не замерена; перекрытие 330 мм и отметка 2-го этажа +3,230 приняты; проект КР — задание (К-2); наружные стены 400 мм, перегородки 120 мм приняты (в брифе толщин нет) (К-1); разрешённая мощность 15 кВт принята по типовым ТУ для частного дома (К-4); подрайон климата не задан — принят не северный (жилые от 2,5 м) (К-7).

Знак «*» — принято, не замерено и не подтверждено (замерить на объекте): К-1: окно пом. 1 (стена А), 2 (А), 3 (В) — окно: место, ширина, высота и подоконник приняты по брифу, стена — по раскладке проектировщика (К-1), не замерены; дверь пом. 1 (стена Б), 3 (Б), 4 (В), 5 (А) — проём: место и ширина приняты проектировщиком по брифу (раскладка этажей — К-1), не замерены; дверь пом. 5 (стена В) — входная дверь: место и ширина проёма приняты проектировщиком по брифу (без плана дома), не замерены; К-3: Л-1 — место, тип и размеры лестницы брифом не заданы (только «лестница из холла 1-го этажа»): одномаршевая 17 × 190 × 250 вдоль стены Б холла — предложение проектировщика; конструкция и расчёт — проект КР; К-5: Ст К1-1, Ст В1-1, Ст Т3-1, Ст К1-2 (кухня), Ст В1-2, Ст Т3-2 — положение стояка принято проектировщиком (проект ВК дома не передан), не замерено.

Знак «**» — предложение проектировщика, заказчиком не утверждено (согласовать с заказчиком): ИЗ-2: ЩС — щит слаботочный: место и состав.

См. лист открытых вопросов (лист 7, записи К-1–К-5; лист 8, запись К-7; лист 9, запись ИЗ-2).

Примечания

1. За отметку 0,000 принят уровень чистого пола. Высоты Н — от чистого пола до оси изделия; привязки — от чистовой грани стены до оси механизма (у рамки на несколько постов — до оси рамки).
2. Розеточные и мокрые линии — через УЗО или дифавтомат с током утечки не более 30 мА (ПУЭ 7.1.79); в санузле выполнить ДСУП (ПУЭ 7.1.87–7.1.88).
3. Кабель — медный, исполнение нг(А)-LS (ГОСТ 31565-2012); скрытая прокладка только горизонтально и вертикально, фактические трассы зафиксировать исполнительной схемой до закрытия отделкой.
4. Расчёт нагрузок, токов КЗ, селективности и сечений — по проекту ЭОМ организации с допуском СРО; лист задаёт состав, расположение и группы.
5. Длины — по плану: от щита вверх в потолочное пространство, по дверям и коридору без захода в мокрые помещения к распределительной коробке над дверью, далее к точкам; вертикали считаются вниз и обратно (у последней точки цепочки — в один конец); запас 10 %. Трассы принципиальные: фактическую зафиксировать исполнительной схемой до закрытия отделкой.
6. Несущие стены не определены: штробы в стенах не выполнять. Маршрут проложен без штроб: горизонтали — за потолком в гофре (133,6 м) и в кабель-канале плинтуса (86,1 м), вертикали — в коробе или накладном канале (115,2 м кабеля). Точек: за потолком — 39, спуск из потолка — 6, по плинтусу — 14, плинтус и подъём — 23.
7. Вариант со штробами — работа после технического заключения: 81,89 м вертикальных штроб от потолка до каждой настенной точки; условие — только после технического заключения: стена не несущая (или вертикальная штроба в несущей согласована конструктором), глубина и ширина 20–25 мм, не в зонах 0–2 ванной. Без заключения и согласования конструктора в смету и в график эта работа не входит.
8. В данных проекта (журнал щита) длины кабеля внесены оценкой (743 м), по трассам из геометрии — 348 м (-53 %): к закупке и в смету принимать длины по трассам, а оценку в данных проекта заменить.
9. Слаботочные сети: кабели и точки считаются по лучам от ЩС** (лист слаботочных сетей): 71 м, портов патч-панели и коммутатора не менее 4; из точек 2 предложения листа слаботочки, не подтверждённые заказчиком. Изделия — в ведомости изделий.

1000 мм · печать 1:1

Изм.	Кол.уч	Лист	№ док.	Подп.	Дата
Разраб.		Кырлан А.С.			04.11.26
Пров.					
ГИП					
Н. контр.					
Утв.					

ГД-2026-012-АИ

Дом 120 м²

Общая площадь 147,36* м² · * размеры приняты, не замерены (реестр — л. 7–9, К-1)

Дизайн-проект интерьера

Стадия	Лист	Листов
РП	44	175

План принципиальных трасс · 1-й этаж

М 1:75


Кырлан Александр Сергеевич

выпуск 04.11.2026 № 4dfa962484 · стр. 46 из 180

План принципиальных трасс · 2-й этаж

Силовые трассы и объёмы электромонтажа, слаботочка в объёмах · размеры в мм

ПРЕДВАРИТЕЛЬНО · не для производства работ · открыто пунктов: 11 (реестр — л. 7–9)

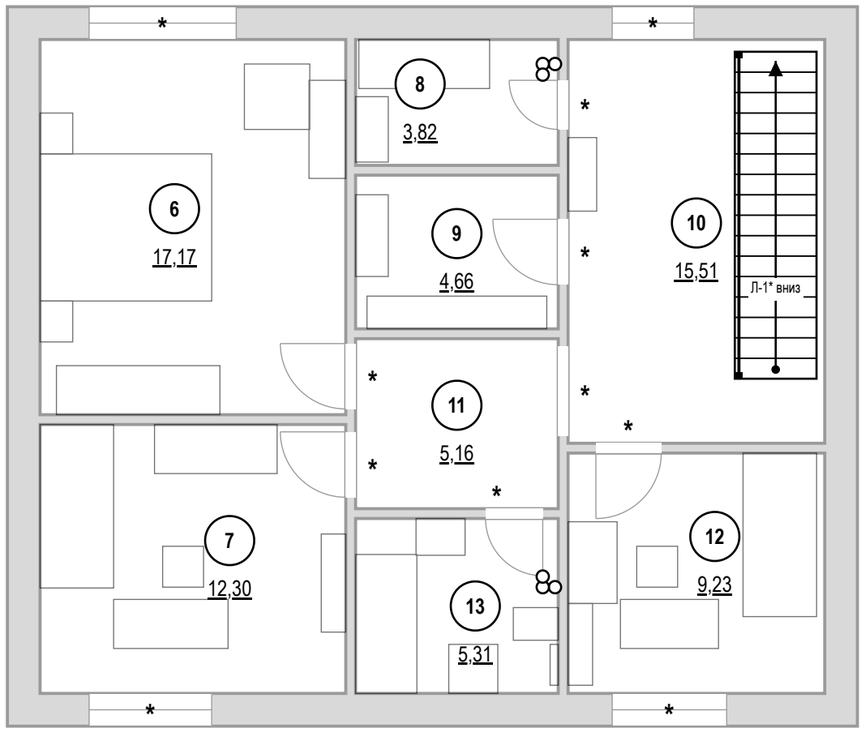

Трассы не построены

нет точки щита квартирного (points kind: panel) — трассу строить не от чего

Экспликация помещений

№	Помещение	Площадь, м²
6	Спальня родителей	17,17
7	Детская	12,30
8	Гардеробная	3,82
9	Кладовая	4,66
10	Холл второго этажа	15,51
11	Коридор второго этажа	5,16
12	Детская вторая	9,23
13	Санузел второго этажа	5,31
	Итого по этажу	73,16

Условные обозначения

- ЩК — щит квартирный
- РК — распределительная коробка над дверью помещения
- магистраль от щита к РК: потолочное пространство, гофра
- мебель и сантехприборы — подложка

Допущения и предложения на листе

Основа листа: взаимное расположение помещений, контур дома 9600 × 8000 и раскладка этажей подобраны проектировщиком под габариты помещений брифа; обмер и проект АР — задание (К-1); высота потолка 2900 мм — по брифу, не замерена; перекрытие 330 мм и отметка 2-го этажа +3,230 приняты; проект КР — задание (К-2); наружные стены 400 мм, перегородки 120 мм приняты (в брифе толщин нет) (К-1); разрешённая мощность 15 кВт принята по типовым ТУ для частного дома (К-4); подрайон климата не задан — принят не северный (жилые от 2,5 м) (К-7).
Знак «*» — принято, не замерено и не подтверждено (замерить на объекте): К-1: окно пом. 6 (стена А), 7 (В), 10 (А), 12 (В) — окно: место, ширина, высота и подоконник приняты по брифу, стена — по раскладке проектировщика (К-1), не замерены; дверь пом. 6 (стена Б), 7 (Б), 8 (Б), 9 (Б), 11 (Б), 12 (А) — проём: место и ширина приняты проектировщиком по брифу (раскладка этажей — К-1), не замерены; дверь пом. 13 (стена А) — Петли у правого откоса (х 6150, у стояков): открытое полотно стоит вдоль стены Б, вошедший идёт влево к умывальнику и ванне; К-2: отметка чистого пола этажа «2-й этаж» +3,230 — отметка чистого пола 2-го этажа +3,230 принята: высота потолка 2900 по брифу + перекрытие с полом 330 (конструкция перекрытия не задана; проект КР — задание); К-3: Л-1 — место, тип и размеры лестницы брифом не заданы (только «лестница из холла 1-го этажа»): одномаршевая 17 × 190 × 250 вдоль стены Б холла — предложение проектировщика; конструкция и расчёт — проект КР; К-5: Ст К1-1, Ст В1-1, Ст Т3-1, Ст К1-2 (кухня), Ст В1-2, Ст Т3-2 — положение стояка принято проектировщиком (проект ВК дома не передан), не замерено.
См. лист открытых вопросов (лист 7, записи К-1–К-5; лист 8, запись К-7).

Примечания

1. За отметку 0,000 принят уровень чистого пола. Высоты Н — от чистого пола до оси изделия; привязки — от чистовой грани стены до оси механизма (у рамки на несколько постов — до оси рамки).
2. Розеточные и мокрые линии — через УЗО или дифавтомат с током утечки не более 30 мА (ПУЭ 7.1.79); в санузле выполнить ДСУП (ПУЭ 7.1.87–7.1.88).
3. Кабель — медный, исполнение нг(А)-LS (ГОСТ 31565-2012); скрытая прокладка только горизонтально и вертикально, фактические трассы зафиксировать исполнительной схемой до закрытия отделкой.
4. Расчёт нагрузок, токов КЗ, селективности и сечений — по проекту ЭОМ организации с допуском СРО; лист задаёт состав, расположение и группы.
5. Щит квартиры (дома) — на 1-м этаже: кабели групп 2-й этаж поднимаются от щита в вертикальном кабель-канале (коробе) у лестницы и далее за потолком к точкам. Место короба и проход через перекрытие — задание конструктору; длины трасс этажа считаются после этого решения.

1000 мм · печать 1:1

Изм.	Кол.уч	Лист	№ док.	Подп.	Дата
Разраб.		Кырлан А.С.			04.11.26
Пров.					
ГИП					
Н. контр.					
Утв.					

ГД-2026-012-АИ

Дом 120 м²

Общая площадь 147,36* м² · * размеры приняты, не замерены (реестр — л. 7–9, К-1)

Дизайн-проект интерьера

Стадия	Лист	Листов
РП	45	175

План принципиальных трасс · 2-й этаж

М 1:75


Кырлан Александр Сергеевич

выпуск 04.11.2026 № 4dfa962484 · стр. 47 из 180

План слаботочных сетей · 1-й этаж

Интернет, ТВ, домофон · размеры в мм · высоты от чистого пола

ПРЕДВАРИТЕЛЬНО · не для производства работ · открыто пунктов: 11 (реестр — л. 7–9)

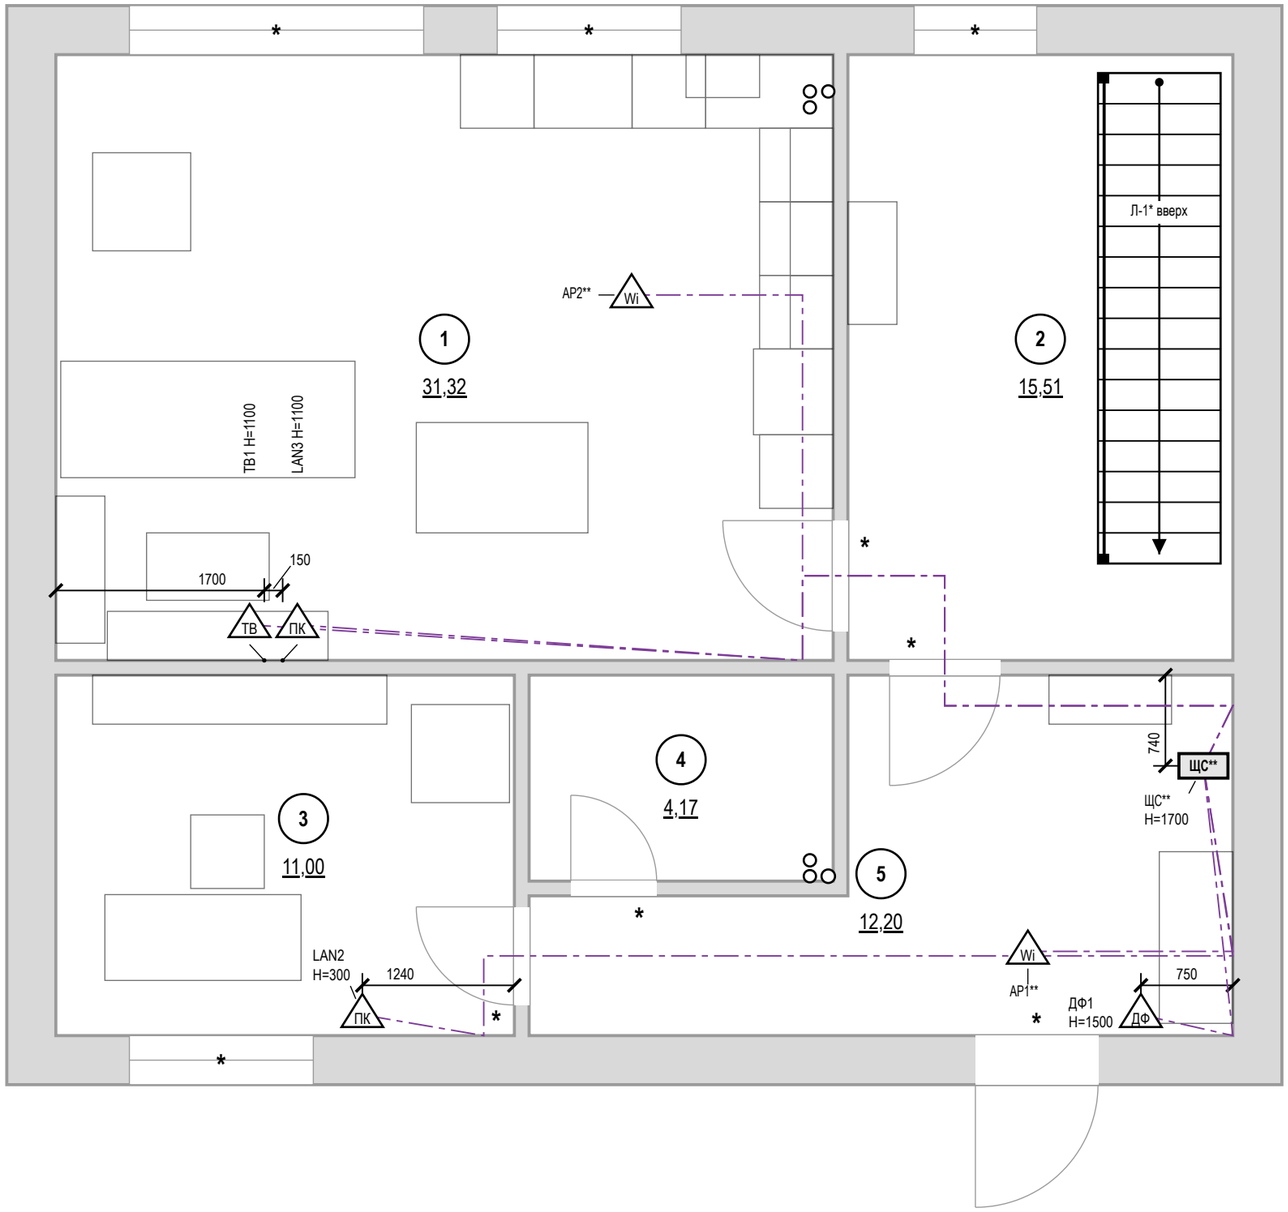

Ведомость слаботочных точек

Марка	Пом.	Назначение	H, мм	Кабель
TB1	1	розетка ТВ	1100	RG-6
LAN3	1	розетка LAN (RJ45)	1100	U/UTP кат. 6
АР2**	1	точка доступа Wi-Fi		U/UTP кат. 6
LAN2	3	розетка LAN (RJ45)	300	U/UTP кат. 6
ЩС**	5	щит слаботочный	1700	ввод пров.
ДФ1	5	домофон (трубка)	1500	по системе
АР1**	5	точка доступа Wi-Fi		U/UTP кат. 6

Условные обозначения

- **ЩС** — щит слаботочный: ввод провайдера, роутер, коммутатор
- ПК — розетка компьютерная RJ45
- ТВ — розетка телевизионная
- ДФ — трубка или монитор домофона
- Wi — точка доступа Wi-Fi (питание PoE)
- кабель от ЩС до точки, отдельным лучом
- мебель и сантехприборы — подложка
- стояк: К1 — канализация, В1 — ХВС, Т3 — ГВС
- 1 — номер помещения, площадь м²

Допущения и предложения на листе

Основа листа: взаимное расположение помещений, контур дома 9600 × 8000 и раскладка этажей подобраны проектировщиком под габариты помещений брифа; обмер и проект АР — задание (К-1); высота потолка 2900 мм — по брифу, не замерена; перекрытие 330 мм и отметка 2-го этажа +3,230 приняты; проект КР — задание (К-2); наружные стены 400 мм, перегородки 120 мм приняты (в брифе толщин нет) (К-1); разрешённая мощность 15 кВт принята по типовым ТУ для частного дома (К-4); подрайон климата не задан — принят не северный (жилые от 2,5 м) (К-7).

Знак «*» — принято, не замерено и не подтверждено (замерить на объекте): К-1: окно пом. 1 (стена А), 2 (А), 3 (В) — окно: место, ширина, высота и подоконник приняты по брифу, стена — по раскладке проектировщика (К-1), не замерены; дверь пом. 1 (стена Б), 3 (Б), 4 (В), 5 (А) — проём: место и ширина приняты проектировщиком по брифу (раскладка этажей — К-1), не замерены; дверь пом. 5 (стена В) — входная дверь: место и ширина проёма приняты проектировщиком по брифу (без плана дома), не замерены; К-3: Л-1 — место, тип и размеры лестницы брифом не заданы (только «лестница из холла 1-го этажа»): одномаршевая 17 × 190 × 250 вдоль стены Б холла — предложение проектировщика; конструкция и расчёт — проект КР; К-5: Ст К1-1, Ст В1-1, Ст Т3-1, Ст К1-2 (кухня), Ст В1-2, Ст Т3-2 — положение стояка принято проектировщиком (проект ВК дома не передан), не замерено.

Знак «**» — предложение проектировщика, заказчиком не утверждено (согласовать с заказчиком): АР2, АР1 — точка доступа Wi-Fi: число и места; ИЗ-2: ЩС — щит слаботочный: место и состав.

См. лист открытых вопросов (лист 7, записи К-1–К-5; лист 8, запись К-7; лист 9, запись ИЗ-2).

Примечания

1. За отметку 0,000 принят уровень чистого пола. Высоты Н — от чистого пола до оси изделия; привязки — от чистовой грани стены до оси механизма (у рамки на несколько постов — до оси рамки).
2. Высота установки, не указанная на плане: розетки LAN и ТВ — 300 мм от чистого пола.
3. Слаботочные кабели — отдельно от силовых: в своей трубе или лотке, при параллельной прокладке не ближе 100 мм к силовым, пересечения под прямым углом; каждую точку — отдельным кабелем от ЩС** без скруток.
4. Трассы на листе — принципиальные; фактические зафиксировать исполнительной схемой до закрытия отделкой. Силовые линии, УЗО 30 мА, ДСУП, кабель нг(А)-LS — по листам розеток и щита.
5. Проект силовой части и расчёт токов КЗ — по проекту ЭОМ; слаботочная часть согласуется с провайдером (ввод в дом, место ONT) и с заказчиком (вызывная панель у калитки, антенна или спутниковое ТВ).

1000 мм · печать 1:1

Изм.	Кол.уч	Лист	№ док.	Подп.	Дата
Разраб.		Кырлан А.С.			04.11.26
Пров.					
ГИП					
Н. контр.					
Утв.					

ГД-2026-012-АИ

Дом 120 м²

Общая площадь 147,36* м² · * размеры приняты, не замерены (реестр — л. 7–9, К-1)

Дизайн-проект интерьера	Стадия	Лист	Листов
	РП	46	175

План слаботочных сетей · 1-й этаж

М 1:50


Кырлан Александр Сергеевич

выпуск 04.11.2026 № 4dfa962484 · стр. 48 из 180

План слаботочных сетей · 2-й этаж

Интернет, ТВ, домофон · размеры в мм · высоты от чистого пола

ПРЕДВАРИТЕЛЬНО · не для производства работ · открыто пунктов: 11 (реестр — л. 7–9)

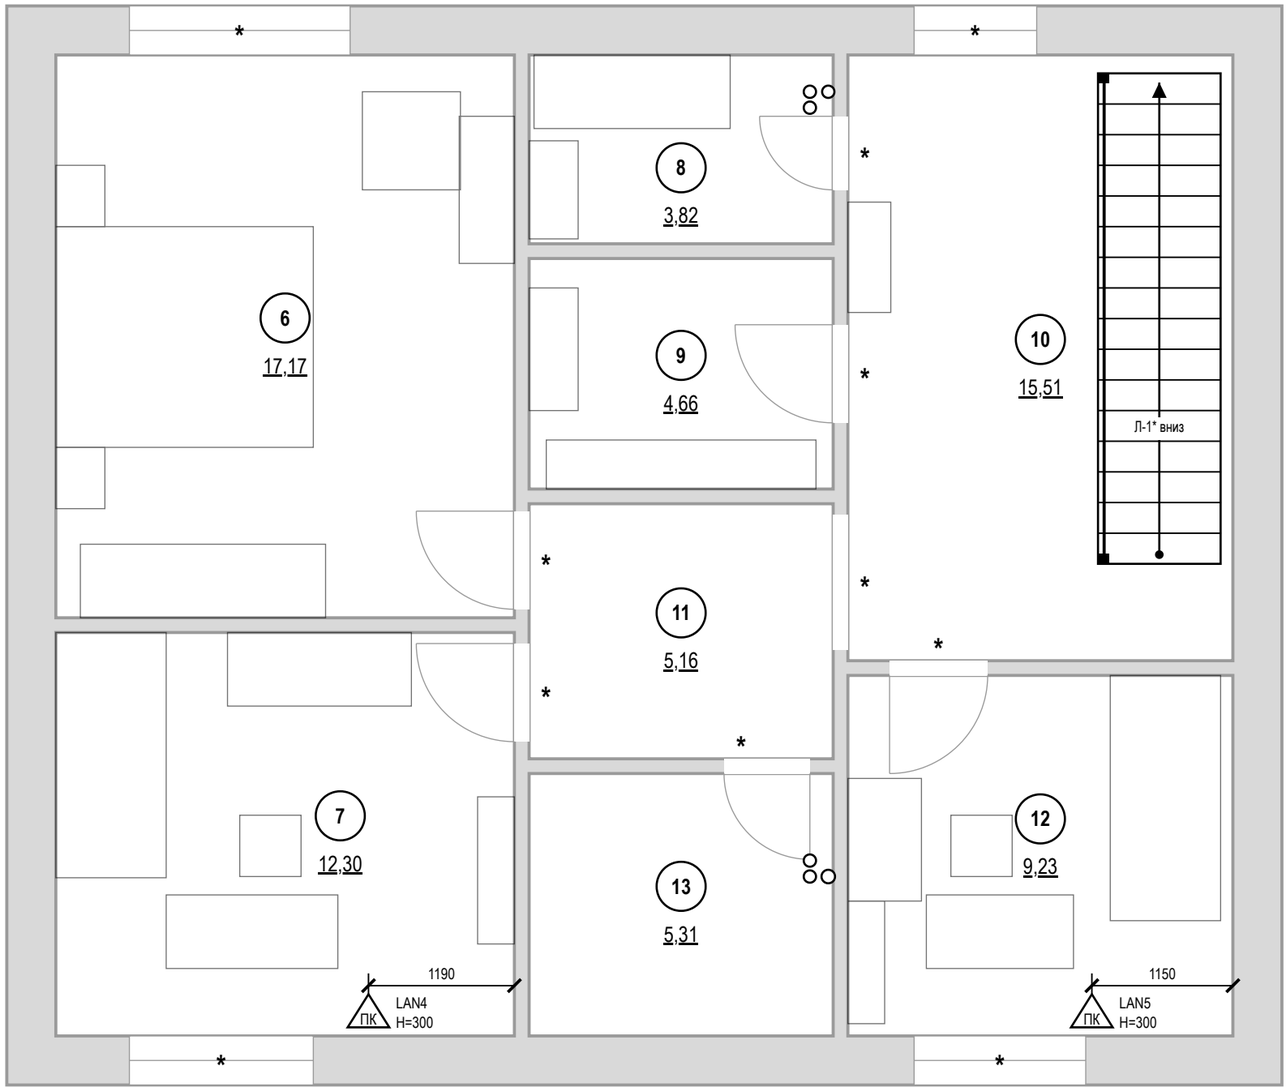

Ведомость слаботочных точек

Марка	Пом.	Назначение	H, мм	Кабель
LAN4	7	розетка LAN (RJ45)	300	U/UTP кат. 6
LAN5	12	розетка LAN (RJ45)	300	U/UTP кат. 6

Условные обозначения

- ПК — розетка компьютерная RJ45
- мебель и сантехприборы — подложка
- стояк: К1 — канализация, В1 — ХВС, Т3 — ГВС
- 1 — номер помещения, площадь м²

Допущения и предложения на листе

Основа листа: взаимное расположение помещений, контур дома 9600 × 8000 и раскладка этажей подобраны проектировщиком под габариты помещений брифа; обмер и проект АР — задание (К-1); высота потолка 2900 мм — по брифу, не замерена; перекрытие 330 мм и отметка 2-го этажа +3,230 приняты; проект КР — задание (К-2); наружные стены 400 мм, перегородки 120 мм приняты (в брифе толщин нет) (К-1); разрешённая мощность 15 кВт принята по типовым ТУ для частного дома (К-4); подрайон климата не задан — принят не северный (жилые от 2,5 м) (К-7).

Знак «*» — принято, не замерено и не подтверждено (замерить на объекте): К-1: окно пом. 6 (стена А), 7 (В), 10 (А), 12 (В) — окно: место, ширина, высота и подоконник приняты по брифу, стена — по раскладке проектировщика (К-1), не замерены; дверь пом. 6 (стена Б), 7 (Б), 8 (Б), 9 (Б), 11 (Б), 12 (А) — проём: место и ширина приняты проектировщиком по брифу (раскладка этажей — К-1), не замерены; дверь пом. 13 (стена А) — Петли у правого откоса (х 6150, у стояков): открытое полотно стоит вдоль стены Б, вошедший идёт влево к умывальнику и ванне; К-2: отметка чистого пола этажа «2-й этаж» +3,230 — отметка чистого пола 2-го этажа +3,230 принята: высота потолка 2900 по брифу + перекрытие с полом 330 (конструкция перекрытия не задана; проект КР — задание); К-3: Л-1 — место, тип и размеры лестницы брифом не заданы (только «лестница из холла 1-го этажа»): одномаршевая 17 × 190 × 250 вдоль стены Б холла — предложение проектировщика; конструкция и расчёт — проект КР; К-5: Ст К1-1, Ст В1-1, Ст Т3-1, Ст К1-2 (кухня), Ст В1-2, Ст Т3-2 — положение стояка принято проектировщиком (проект ВК дома не передан), не замерено.

Знак «**» — предложение проектировщика, заказчиком не утверждено (согласовать с заказчиком): ИЗ-2: ЩС — щит слаботочный: место и состав.

См. лист открытых вопросов (лист 7, записи К-1–К-5; лист 8, запись К-7; лист 9, запись ИЗ-2).

Примечания

1. За отметку 0,000 принят уровень чистого пола. Высоты H — от чистого пола до оси изделия; привязки — от чистовой грани стены до оси механизма (у рамки на несколько постов — до оси рамки).
2. Высота установки, не указанная на плане: розетки LAN и ТВ — 300 мм от чистого пола.
3. Слаботочные кабели — отдельно от силовых: в своей трубе или лотке, при параллельной прокладке не ближе 100 мм к силовым, пересечения под прямым углом; каждую точку — отдельным кабелем от ЩС** без скруток.
4. Трассы на листе — принципиальные; фактические зафиксировать исполнительной схемой до закрытия отделкой. Силовые линии, УЗО 30 мА, ДСУП, кабель нг(А)-LS — по листам розеток и щита.
5. Проект силовой части и расчёт токов КЗ — по проекту ЭОМ; слаботочная часть согласуется с провайдером (ввод в дом, место ONT) и с заказчиком (вызывная панель у калитки, антенна или спутниковое ТВ).

1000 мм · печать 1:1

Изм.	Кол.уч	Лист	№ док.	Подп.	Дата
Разраб.		Кырлан А.С.			04.11.26
Пров.					
ГИП					
Н. контр.					
Утв.					

ГД-2026-012-АИ

Дом 120 м²

Общая площадь 147,36* м² · * размеры приняты, не замерены (реестр — л. 7–9, К-1)

Дизайн-проект интерьера

Стадия	Лист	Листов
РП	47	175

План слаботочных сетей · 2-й этаж


М 1:50

Кырлан Александр Сергеевич

выпуск 04.11.2026 № 4dfa962484 · стр. 49 из 180

План вентиляции · 1-й этаж

Вытяжка, приток, переток · кондиционирование не предусмотрено · размеры в мм · высоты от чистого пола

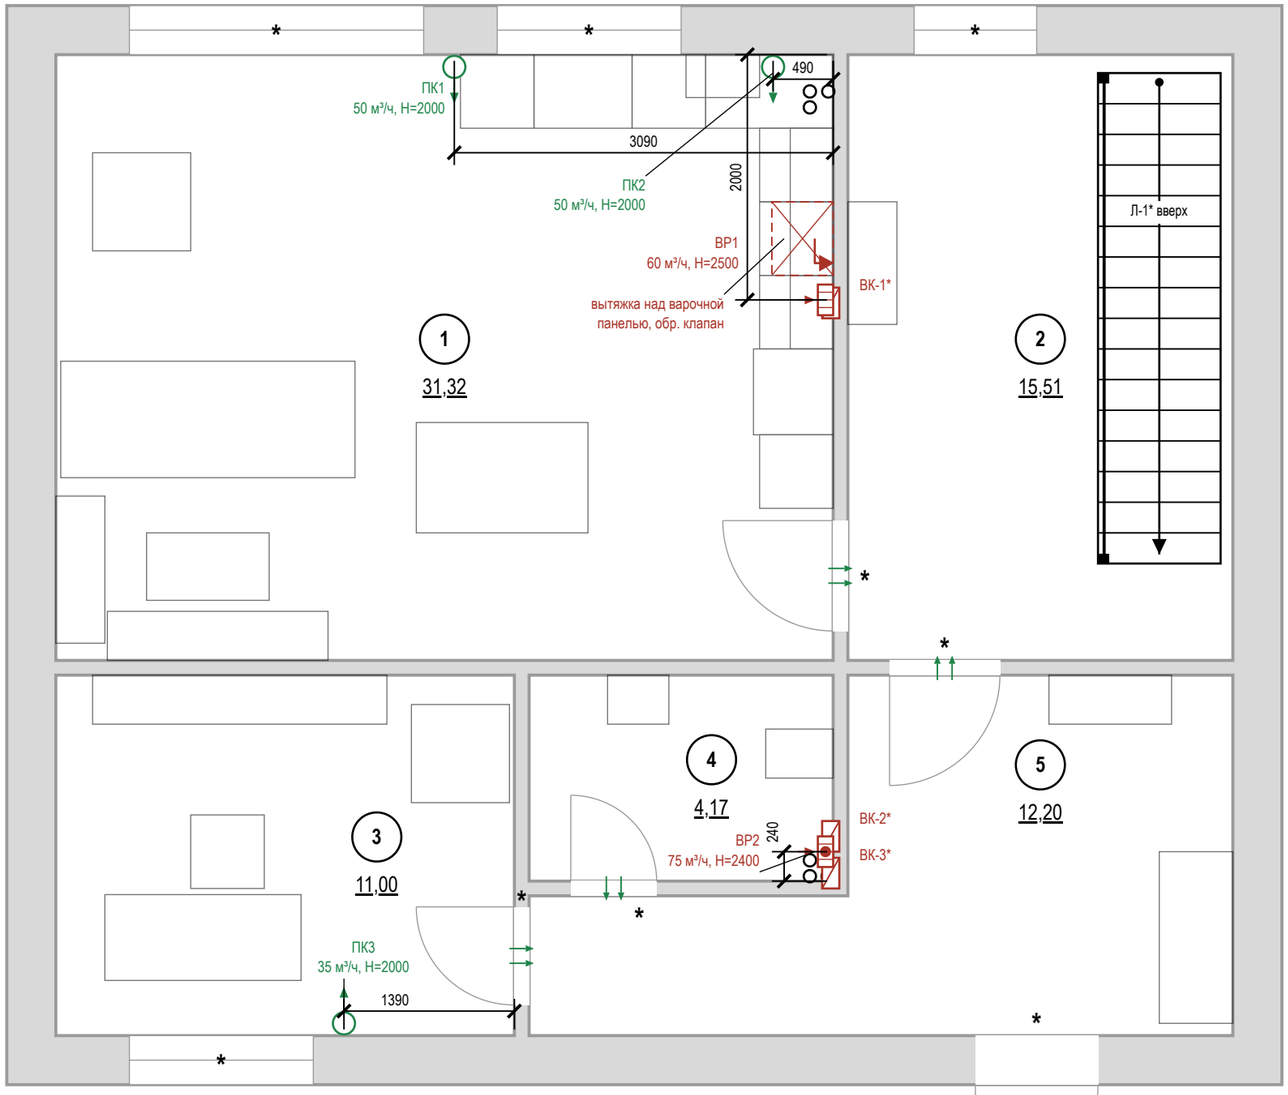

Условные обозначения

- стояк: К1 — канализация, В1 — ХВС, Т3 — ГВС
- номер помещения, площадь м²
- вытяжная решётка в вентканал: марка, расход м³/ч, H центра от чистого пола
- вытяжная решётка с бытовым вентилятором и обратным клапаном: марка, расход, H
- приточный клапан (КИВ) в наружной стене: марка, расход, H центра
- переток: зазор под полотном или переточная решётка
- кухонная вытяжка над варочной панелью
- вентканал ВК-N; «*» — принят до обмера
- воздуховод кухонной вытяжки в коробе под потолком
- отдельный вход воздуховода в вентканал, обратный клапан
- * — «*» — принято, не замерено и не подтверждено

Воздухообмен, м³/ч

№	Помещение	Выт. норма	Выт. проект	Прит. норма	Прит. проект	Устрой-ства
1	Гостиная-кухня	60	60	91	100	ВР1, ПК1, ПК2
3	Кабинет			32	35	ПК3
4	Санузел гостевой	25	75			ВР2
	Итого	**85**	**135**	**123**	**135**	

Воздухообмен этажа — по большей из сумм притока и вытяжки: норма 123 м³/ч, проект 135 м³/ч.
Вытяжка не меньше притока — баланс сведён.

Привязки — до обмера
Вентканалы ВК-N* приняты проектировщиком, решётки и воздуховоды — от них. До черновых работ — обмер каналов и тяги, лист перевыпустить по факту.

Примечания

1. Расчёт систем ОВ и подбор оборудования — проектная организация с допуском СРО; лист даёт места, трассы и привязки.
2. Нормы одноквартирного дома — СП 55.13330.2016, п. 9.7: в жилых комнатах не менее однократного воздухообмена в час, из кухни не менее 60 м³/ч, из ванной, туалета, совмещённого санузла не менее 25 м³/ч; кухня с газовой плитой — 100 м³/ч в запас. Системы — по СП 60.13330.2020.
3. Вентканалы и шахты не сужать, не переносить и не закрывать; вентилятор и кухонная вытяжка — через обратный клапан, без перекрытия естественной тяги.
4. Проектные расходы — не ниже нормы, вытяжка сведена с притоком вентиляторами мокрых помещений. Клапаны — в простенке у окна, центр 2000 мм, не над кроватью, не ближе 300 мм к стоякам отопления; типоразмер — на расход.
5. Кухонная вытяжка в воздухообмен не включена: воздуховод не менее Ø125 в коробе, вход в канал отдельный.
6. Переток — зазор под полотнами межкомнатных дверей или переточная решётка.
7. Кондиционирование заданием не предусмотрено; при установке трассы фреона и дренажа (не менее 40 мм/м, в К1 через сифон) и питание заложить до черновых работ.
8. Привязки оборудования — по паспортам приобретённых моделей, до черновых работ.
9. Знак «*» у проёма — допущение: положение проёма не замерено (окно пом. 1, стена А (2 шт.); дверь пом. 1, стена Б; окно пом. 2, стена А; окно пом. 3, стена В; дверь пом. 3, стена Б; дверь пом. 4, стена В; и ещё 2); размер напечатан как принятый. Реестр: листы 7–9, вопросы К-1, К-8.
10. Клапаны ПК1, ПК2, ПК3 выведены в простенок у окна, положение которого — допущение (знак «*»): после обмера окна привязку сверить.

1000 мм · печать 1:1

Допущения и предложения на листе. Основа листа: взаимное расположение помещений, контур дома 9600 × 8000 и раскладка этажей подобраны проектировщиком под габариты помещений брифа; обмер и проект АР — задание (К-1); высота потолка 2900 мм — по брифу, не замерена; перекрытие 330 мм и отметка 2-го этажа +3,230 приняты; проект КР — задание (К-2); наружные стены 400 мм, перегородки 120 мм приняты (в брифе толщин нет) (К-1); разрешённая мощность 15 кВт принята по типовым ТУ для частного дома (К-4); подрайон климата не задан — принят не северный (жилые от 2,5 м) (К-7). Знак «*» — принято, не замерено (замерить): К-3: Л-1; К-5: Ст К1-1, Ст В1-1, Ст Т3-1, Ст К1-2 (кухня), Ст В1-2, Ст Т3-2. См. лист открытых вопросов (лист 7, записи К-1–К-5; лист 8, запись К-7).

Изм.	Кол.уч	Лист	№ док.	Подп.	Дата
Разраб.		Кырлан А.С.			04.11.26
Пров.					
ГИП					
Н. контр.					
Утв.					

ГД-2026-012-АИ

Дом 120 м²

Общая площадь 147,36* м² · * размеры приняты, не замерены (реестр — л. 7–9, К-1)

Дизайн-проект интерьера

Стадия	Лист	Листов
РП	48	175

План вентиляции · 1-й этаж

М 1:50


Кырлан Александр Сергеевич

ПРЕДВАРИТЕЛЬНО · не для производства работ · открыто пунктов: 11 (реестр — л. 7–9)

выпуск 04.11.2026 № 4dfa962484 · стр. 50 из 180

План вентиляции · 2-й этаж

Вытяжка, приток, переток · кондиционирование не предусмотрено · размеры в мм · высоты от чистого пола

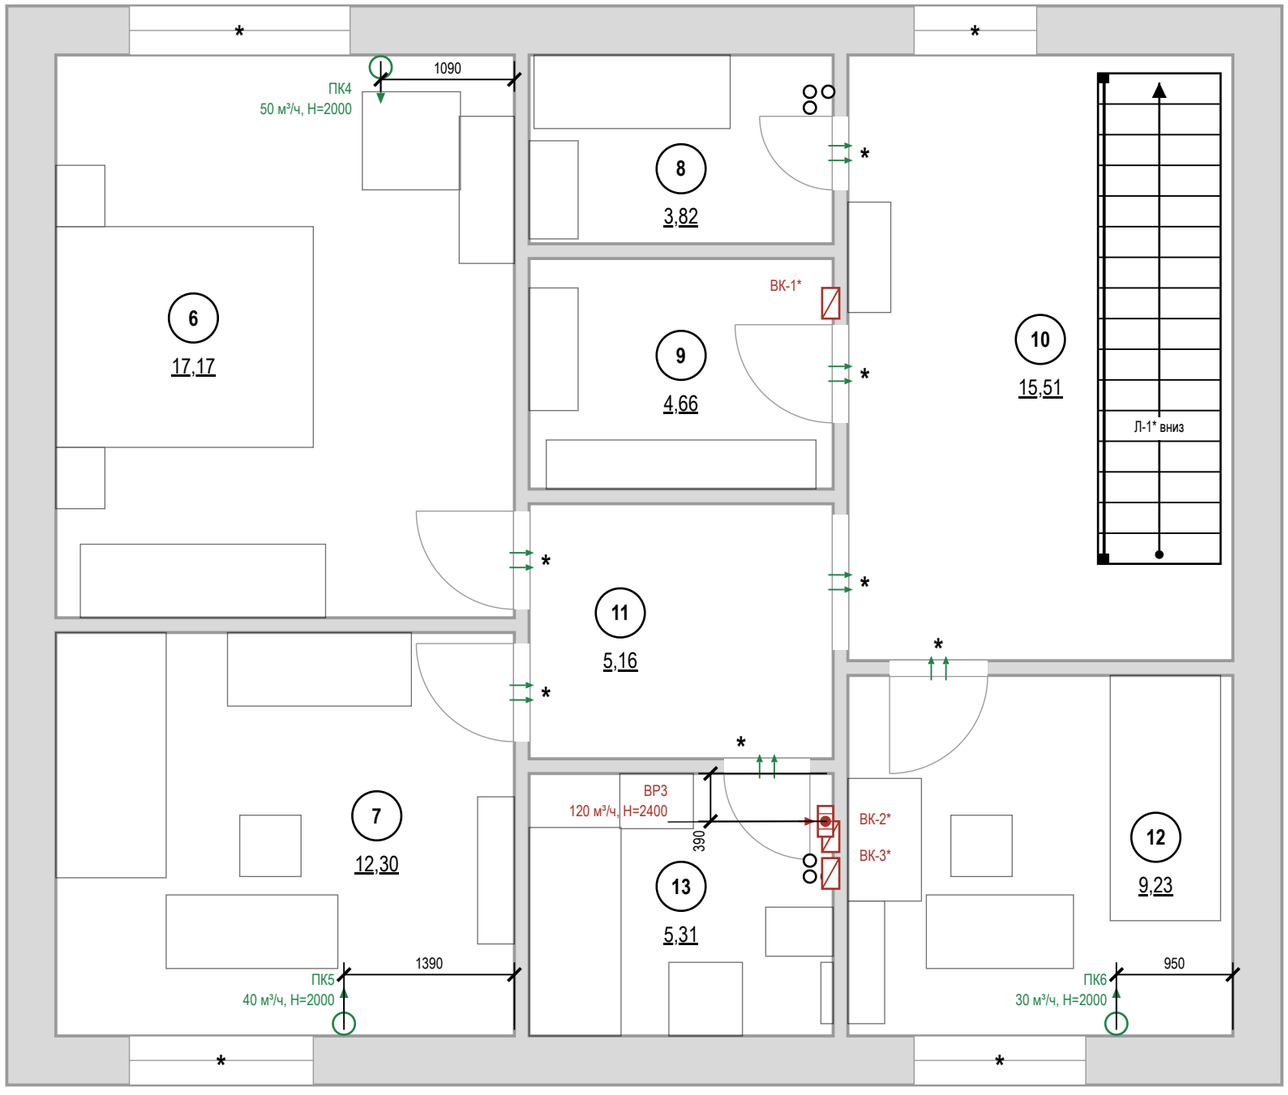

Примечания

1. Расчёт систем ОВ и подбор оборудования — проектная организация с допуском СРО; лист даёт места, трассы и привязки.
2. Нормы одноквартирного дома — СП 55.13330.2016, п. 9.7: в жилых комнатах не менее однократного воздухообмена в час, из кухни не менее 60 м³/ч, из ванной, туалета, совмещённого санузла не менее 25 м³/ч; кухня с газовой плитой — 100 м³/ч в запас. Системы — по СП 60.13330.2020.
3. Вентканалы и шахты не сужать, не переносить и не закрывать; вентилятор и кухонная вытяжка — через обратный клапан, без перекрытия естественной тяги.
4. Проектные расходы — не ниже нормы, вытяжка сведена с притоком вентиляторами мокрых помещений. Клапаны — в простенке у окна, центр 2000 мм, не над кроватью, не ближе 300 мм к стоякам отопления; типоразмер — на расход.
5. Переток — зазор под полотнами межкомнатных дверей или переточная решётка.
6. Кондиционирование заданием не предусмотрено; при установке трассы фреона и дренажа (не менее 40 мм/м, в К1 через сифон) и питание заложить до черновых работ.
7. Привязки оборудования — по паспортам приобретённых моделей, до черновых работ.
8. Знак «*» у проёма — допущение: положение проёма не замерено (окно пом. 6, стена А; дверь пом. 6, стена Б; окно пом. 7, стена В; дверь пом. 7, стена Б; дверь пом. 8, стена Б; дверь пом. 9, стена Б; и ещё 5); размер напечатан как принятый. Реестр: листы 7–9, вопросы К-1, К-9.
9. Клапаны ПК4, ПК5, ПК6 выведены в простенок у окна, положение которого — допущение (знак «*»): после обмера окна привязку сверить.

1000 мм · печать 1:1

ПРЕДВАРИТЕЛЬНО · не для производства работ · открыто пунктов: 11 (реестр — л. 7–9)

Условные обозначения

- стояк: К1 — канализация, В1 — ХВС, Т3 — ГВС
- 1 — номер помещения, площадь м²
- вытяжная решётка с бытовым вентилятором и обратным клапаном: марка, расход, Н
- приточный клапан (КИВ) в наружной стене: марка, расход, Н центра
- переток: зазор под полотном или переточная решётка
- вентканал ВК-N; «*» — принят до обмера
- * — «*» — принято, не замерено и не подтверждено

Воздухообмен, м³/ч

№	Помещение	Выт. норма	Выт. проект	Прит. норма	Прит. проект	Устрой-ства
6	Спальня родителей			50	50	ПК4
7	Детская			36	40	ПК5
8	Гардеробная	2				переток
9	Кладовая	3				переток
12	Детская вторая			27	30	ПК6
13	Санузел второго этажа	25	120			ВР3
	Итого	**30**	**120**	**113**	**120**	

Воздухообмен этажа — по большей из сумм притока и вытяжки: норма 113 м³/ч, проект 120 м³/ч.
Вытяжка не меньше притока — баланс сведён.

Привязки — до обмера
Вентканалы ВК-N* приняты проектировщиком, решётки и воздуховоды — от них. До черновых работ — обмер каналов и тяги, лист перевыпустить по факту.

Допущения и предложения на листе. Основа листа: взаимное расположение помещений, контур дома 9600 × 8000 и раскладка этажей подобраны проектировщиком под габариты помещений брифа; обмер и проект АР — задание (К-1); высота потолка 2900 мм — по брифу, не замерена; перекрытие 330 мм и отметка 2-го этажа +3,230 приняты; проект КР — задание (К-2); наружные стены 400 мм, перегородки 120 мм приняты (в брифе толщин нет) (К-1); разрешённая мощность 15 кВт принята по типовым ТУ для частного дома (К-4); подрайон климата не задан — принят не северный (жилые от 2,5 м) (К-7). Знак «*» — принято, не замерено и не подтверждено (замерить на объекте): К-2: отметка чистого пола этажа «2-й этаж» +3,230 — отметка чистого пола 2-го этажа +3,230 принята: высота потолка 2900 по брифу + перекрытие с полом 330 (конструкция перекрытия не задана; проект КР — задание); К-3: Л-1 — место, тип и размеры лестницы брифом не заданы (только «лестница из холла 1-го этажа»): одномаршевая 17 × 190 × 250 вдоль стены Б холла — предложение проектировщика; конструкция и расчёт — проект КР; К-5: Ст К1-1, Ст В1-1, Ст Т3-1, Ст К1-2 (кухня), Ст В1-2, Ст Т3-2 — положение стояка принято проектировщиком (проект ВК дома не передан), не замерено. См. лист открытых вопросов (лист 7, записи К-1–К-5; лист 8, запись К-7).

Изм.	Кол.уч	Лист	№ док.	Подп.	Дата
Разраб.		Кырлан А.С.			04.11.26
Пров.					
ГИП					
Н. контр.					
Утв.					

ГД-2026-012-АИ

Дом 120 м²

Общая площадь 147,36* м² · * размеры приняты, не замерены (реестр — л. 7–9, К-1)

Дизайн-проект интерьера

Стадия	Лист	Листов
РП	49	175

План вентиляции · 2-й этаж


М 1:50

Кырлан Александр Сергеевич

выпуск 04.11.2026 № 4dfa962484 · стр. 51 из 180

План отопления · 1-й этаж

Радиаторы, стояки, подводки · размеры в мм · высоты от чистого пола

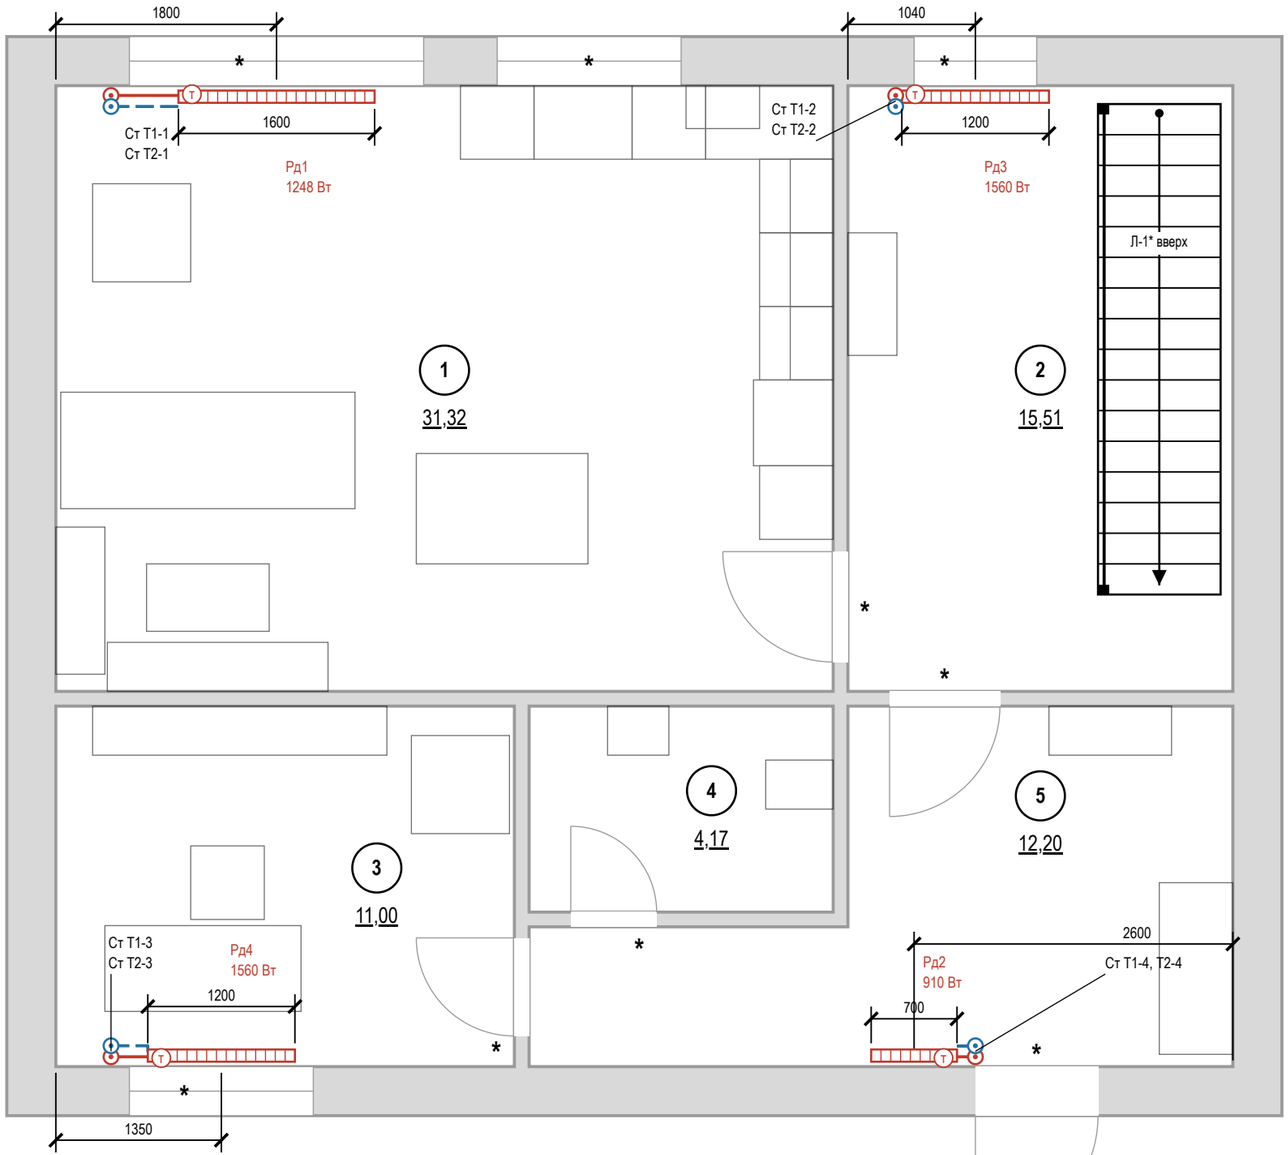

Примечания

1. Расчёт системы отопления, теплопотерь и подбор приборов — проектная организация с допуском СРО; лист даёт места и привязки.
2. Тип, длина и мощность радиаторов — по теплотехническому расчёту; лист задаёт места, зазоры и подключение.
3. Зазоры радиатора: низ не менее 100 мм от чистого пола, верх не менее 100 мм до подоконника, 30–50 мм от стены до задней панели; центр по оси окна с допуском ±20 мм. Верх до подоконника — 300 мм (Рд1 — 100). Радиаторы не закрывать глухими коробами и мебелью; трубы через стены и перекрытия — в гильзах.
4. Источник тепла (котёл: газ / электро / твёрдое топливо), его место и котельная — по решению заказчика; до решения разводка от коллектора к приборам — принципиальная (СП 60.13330.2020).
5. Без отопительного прибора: пом. 4 — внутренние, без наружных стен, окон и дверей наружу, обогреваются от смежных помещений; полотенцесушитель — по листам ВК.
6. Привязки приборов и подводок — по паспортам приобретённых радиаторов и клапанов, до черновых работ.
7. До закрытия отделкой трубопроводы отопления испытать гидростатическим давлением с оформлением акта (СП 73.13330.2016, 7.2–7.3).
8. Знак «*» у проёма — допущение: положение проёма не замерено (окно пом. 1, стена А (2 шт.); дверь пом. 1, стена Б; окно пом. 2, стена А; окно пом. 3, стена В; дверь пом. 3, стена Б; дверь пом. 4, стена В; и ещё 2); размер напечатан как принятый. Реестр: листы 7–9, вопросы К-1, К-8.
9. Радиаторы Рд1, Рд3, Рд4 стоят по оси окна, положение которого — допущение (знак «*»): после обмера окна привязки приборов и подводок сверить.

1000 мм · печать 1:1

ПРЕДВАРИТЕЛЬНО · не для производства работ · открыто пунктов: 11 (реестр — л. 7–9)

Условные обозначения

- (1) — номер помещения, площадь м²
- радиатор отопления (марка РО-N, длина по плану)
- (Т) — клапан с термоголовкой на подаче
- стояк отопления, подающий (Ст Т1-N)
- стояк отопления, обратный (Ст Т2-N)
- Т1 — отопление, подающий трубопровод
- Т2 — отопление, обратный трубопровод
- * — «*» — принято, не замерено и не подтверждено

Ведомость радиаторов

Марка	Помещение	Тип	Д×В×Г, мм	Низ / стена	Q, Вт
Рд1	1. Гостиная-кухня	панельный 22	1600×300×100	100 / 40	1248
Рд3	2. Холл с лестницей	панельный 22	1200×500×100	100 / 40	1560
Рд4	3. Кабинет	панельный 22	1200×500×100	100 / 40	1560
Рд2	5. Прихожая	панельный 22	700×500×100	100 / 40	910

Низ — от чистого пола, стена — зазор до задней панели, мм.

Привязки — до обмера

Подъёмы подводок отопления в исходных данных не заданы: показаны у откосов окон и у торцов приборов принципиально, разводка — от котла через распределительный коллектор. До черновых работ — место котла, коллектора и подъёмов труб и паспорта приборов; лист перевыпустить по факту.

Допущения и предложения на листе. Основа листа: взаимное расположение помещений, контур дома 9600 × 8000 и раскладка этажей подобраны проектировщиком под габариты помещений брифа; обмер и проект АР — задание (К-1); высота потолка 2900 мм — по брифу, не замерена; перекрытие 330 мм и отметка 2-го этажа +3,230 приняты; проект КР — задание (К-2); наружные стены 400 мм, перегородки 120 мм приняты (в брифе толщин нет) (К-1); разрешённая мощность 15 кВт принята по типовым ТУ для частного дома (К-4); подрайон климата не задан — принят не северный (жилые от 2,5 м) (К-7). Знак «*» — принято, не замерено и не подтверждено (замерить на объекте): К-3: Л-1 — место, тип и размеры лестницы брифом не заданы (только «лестница из холла 1-го этажа»): одномаршевая 17 × 190 × 250 вдоль стены Б холла — предложение проектировщика; конструкция и расчёт — проект КР. См. лист открытых вопросов (лист 7, записи К-1–К-4, К-6; лист 8, запись К-7); по листу — К-6.

Изм.	Кол.уч	Лист	№ док.	Подп.	Дата
Разраб.		Кырлан А.С.			04.11.26
Пров.					
ГИП					
Н. контр.					
Утв.					

ГД-2026-012-АИ

Дом 120 м²

Общая площадь 147,36* м² · * размеры приняты, не замерены (реестр — л. 7–9, К-1)

Дизайн-проект интерьера

Стадия	Лист	Листов
РП	50	175

План отопления · 1-й этаж


М 1:50

Кырлан Александр Сергеевич

выпуск 04.11.2026 № 4dfa962484 · стр. 52 из 180

План отопления · 2-й этаж

Радиаторы, стояки, подводки · размеры в мм · высоты от чистого пола

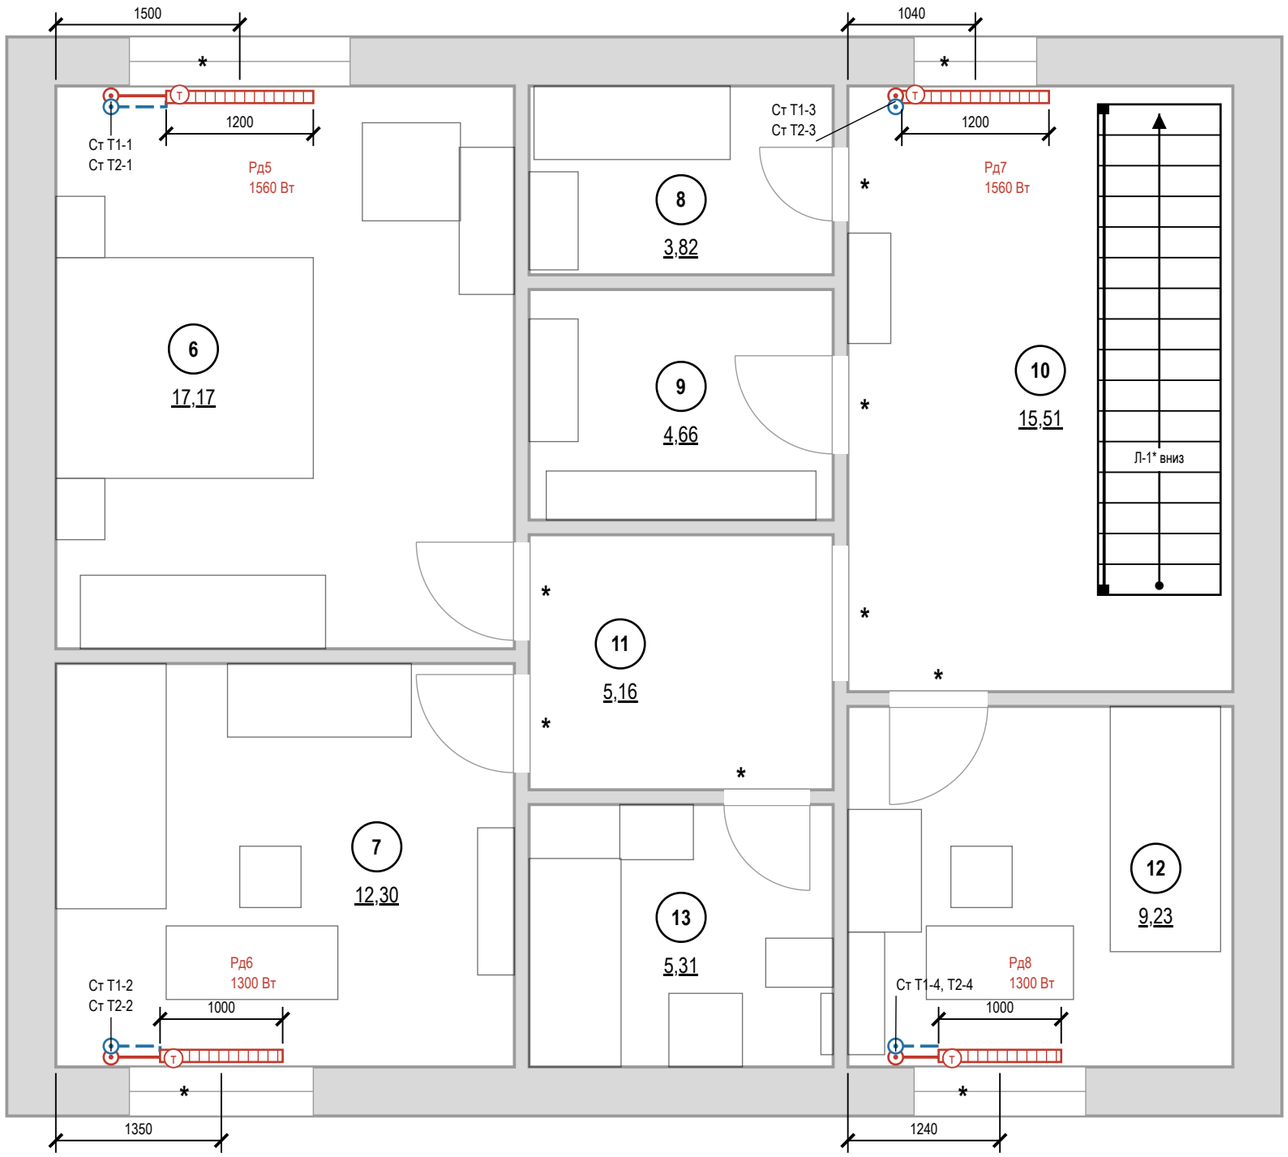

Примечания

1. Расчёт системы отопления, теплопотерь и подбор приборов — проектная организация с допуском СРО; лист даёт места и привязки.
2. Тип, длина и мощность радиаторов — по теплотехническому расчёту; лист задаёт места, зазоры и подключение.
3. Зазоры радиатора: низ не менее 100 мм от чистого пола, верх не менее 100 мм до подоконника, 30–50 мм от стены до задней панели; центр по оси окна с допуском ±20 мм. Верх до подоконника — 300 мм. Радиаторы не закрывать глухими коробами и мебелью; трубы через стены и перекрытия в гильзах.
4. Источник тепла (котёл: газ / электро / твёрдое топливо), его место и котельная — по решению заказчика; до решения разводка от коллектора к приборам — принципиальная (СП 60.13330.2020).
5. Без отопительного прибора: пом. 9, пом. 11 — внутренние, без наружных стен, окон и дверей наружу, обогреваются от смежных помещений; полотенцесушитель — по листам ВК.
6. Прибор не задан: пом. 13 — прибор или тёплый пол по расчёту до черновых работ.
7. Привязки приборов и подводок — по паспортам приобретённых радиаторов и клапанов, до черновых работ.
8. До закрытия отделкой трубопроводы отопления испытать гидростатическим давлением с оформлением акта (СП 73.13330.2016, 7.2–7.3).
9. Знак «*» у проёма — допущение: положение проёма не замерено (окно пом. 6, стена А; дверь пом. 6, стена Б; окно пом. 7, стена В; дверь пом. 7, стена Б; дверь пом. 8, стена Б; дверь пом. 9, стена Б; и ещё 5); размер напечатан как принятый. Реестр: листы 7–9, вопросы К-1, К-9.
10. Радиаторы Рд5, Рд6, Рд7, Рд8 стоят по оси окна, положение которого — допущение (знак «*»): после обмера окна привязки приборов и подводок сверить.

1000 мм · печать 1:1

ПРЕДВАРИТЕЛЬНО · не для производства работ · открыто пунктов: 11 (реестр — л. 7–9)

Условные обозначения

- 1 — номер помещения, площадь м²
- радиатор отопления (марка РО-N, длина по плану)
- Т — клапан с термоголовкой на подаче
- стояк отопления, подающий (Ст Т1-N)
- стояк отопления, обратный (Ст Т2-N)
- Т1 — отопление, подающий трубопровод
- Т2 — отопление, обратный трубопровод
- * — «*» — принято, не замерено и не подтверждено

Ведомость радиаторов

Марка	Помещение	Тип	Д×В×Г, мм	Низ / стена	Q, Вт
Рд5	6. Спальня родителей	панельный 22	1200×500×100	100 / 40	1560
Рд6	7. Детская	панельный 22	1000×500×100	100 / 40	1300
Рд7	10. Холл второго этажа	панельный 22	1200×500×100	100 / 40	1560
Рд8	12. Детская вторая	панельный 22	1000×500×100	100 / 40	1300

Низ — от чистого пола, стена — зазор до задней панели, мм.

Привязки — до обмера

Подъёмы подводок отопления в исходных данных не заданы: показаны у откосов окон принципиально, разводка — от котла через распределительный коллектор. До черновых работ место котла, коллектора и подъёмов труб и паспорта приборов; лист перевыпустить по факту.

Допущения и предложения на листе. Основа листа: взаимное расположение помещений, контур дома 9600 × 8000 и раскладка этажей подобраны проектировщиком под габариты помещений брифа; обмер и проект АР — задание (К-1); высота потолка 2900 мм — по брифу, не замерена; перекрытие 330 мм и отметка 2-го этажа +3,230 приняты; проект КР — задание (К-2); наружные стены 400 мм, перегородки 120 мм приняты (в брифе толщин нет) (К-1); разрешённая мощность 15 кВт принята по типовым ТУ для частного дома (К-4); подрайон климата не задан — принят не северный (жилые от 2,5 м) (К-7). Знак «*» — принято, не замерено и не подтверждено (замерить на объекте): К-2: отметка чистого пола этажа «2-й этаж» +3,230 — отметка чистого пола 2-го этажа +3,230 принята: высота потолка 2900 по брифу + перекрытие с полом 330 (конструкция перекрытия не задана; проект КР — задание); К-3: Л-1 — место, тип и размеры лестницы брифом не заданы (только «лестница из холла 1-го этажа»): одномаршевая 17 × 190 × 250 вдоль стены Б холла — предложение проектировщика; конструкция и расчёт — проект КР. См. лист открытых вопросов (лист 7, записи К-1–К-4, К-6; лист 8, запись К-7); по листу — К-6.

Изм.	Кол.уч	Лист	№ док.	Подп.	Дата
Разраб.		Кырлан А.С.			04.11.26
Пров.					
ГИП					
Н. контр.					
Утв.					

ГД-2026-012-АИ

Дом 120 м²

Общая площадь 147,36* м² · * размеры приняты, не замерены (реестр — л. 7–9, К-1)

Дизайн-проект интерьера

Стадия	Лист	Листов
РП	51	175

План отопления · 2-й этаж

М 1:50

Кырлан Александр Сергеевич


выпуск 04.11.2026 № 4dfa962484 · стр. 53 из 180

План выводов сантехники · 1-й этаж


Выводы В1, Т3, К1 · привязки от чистовых стен · высоты от чистого пола, мм

ПРЕДВАРИТЕЛЬНО · не для производства работ · открыто пунктов: 11 (реестр — л. 7–9)

Фрагмент 1. Санузел гостевой (пом. 4)

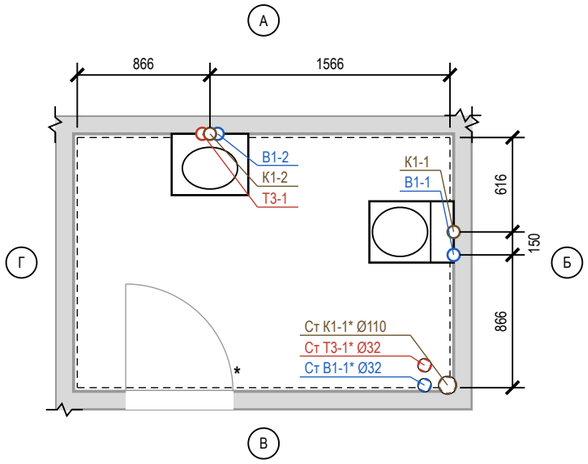

Фрагмент 2. Гостиная-кухня (пом. 1)

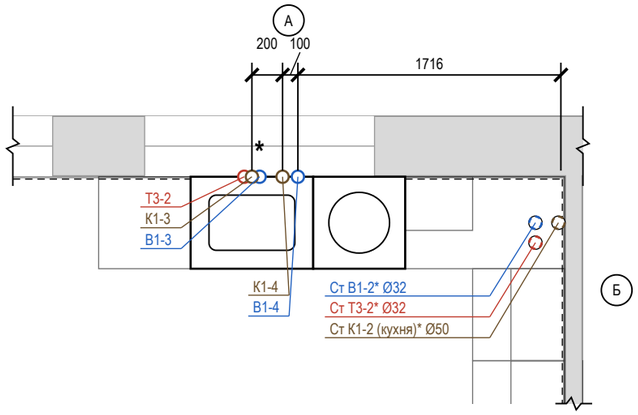

Ведомость привязок выводов

Код	Прибор	Ø	H, мм	Привязка от чист. стен, мм	Прим.
В1-1	Ст1 унитаз подвесной	½"	250*	ст. Б: 766 от А	в раме инсталляции
К1-1	Ст1 унитаз подвесной	Ø110	220*	ст. Б: 616 от А	
В1-2	Ст2 умывальник	½"	600*	ст. А: 916 от Г	межос. 100
Т3-1	Ст2 умывальник	½"	600*	ст. А: 816 от Г	межос. 100
К1-2	Ст2 умывальник	Ø50	500*	ст. А: 866 от Г	
В1-3	Кх2 мойка кухонная	½"	600*	ст. А: 1966 от Б	межос. 100
Т3-2	Кх2 мойка кухонная	½"	600*	ст. А: 2066 от Б	межос. 100
К1-3	Кх2 мойка кухонная	Ø50	400*	ст. А: 2016 от Б	
В1-4	Кх3 посудомоечная машина	½"	550*	ст. А: 1716 от Б	кран ПММ в шкафу мойки
К1-4	Кх3 посудомоечная машина	Ø40	550*	ст. А: 1816 от Б	слив ПММ в шкафу мойки

* — высота по практике монтажа; сверить по паспорту прибора

Условные обозначения

- вывод В1 (код — в ведомости привязок)
- вывод Т3 (код — в ведомости привязок)
- вывод К1 (код — в ведомости привязок)
- сантехприбор по расстановке (габарит модели)
- чистовая поверхность стены (от неё привязки)
- стояк «Ст К1-N / Ст В1-N» (ГОСТ 21.601), Ø мм
- * стояк Т3 не на обмере — принят в шахте рядом со Ст В1, сверить
- линия обрыва (граница фрагмента)
- А — обозначение стены А–Г (как на развёртках)

Допущения и предложения на листе

Основа листа: взаимное расположение помещений, контур дома 9600 × 8000 и раскладка этажей подобраны проектировщиком под габариты помещений брифа; обмер и проект АР — задание (К-1); высота потолка 2900 мм — по брифу, не замерена; перекрытие 330 мм и отметка 2-го этажа +3,230 приняты; проект КР — задание (К-2); наружные стены 400 мм, перегородки 120 мм приняты (в брифе толщин нет) (К-1); разрешённая мощность 15 кВт принята по типовым ТУ для частного дома (К-4); подрайон климата не задан — принят не северный (жилые от 2,5 м) (К-7).

Знак «*» — принято, не замерено и не подтверждено (замерить на объекте): К-1: окно пом. 1 (стена А) — окно: место, ширина, высота и подоконник приняты по брифу, стена — по раскладке проектировщика (К-1), не замерены; дверь пом. 4 (стена В) — проём: место и ширина приняты проектировщиком по брифу (раскладка этажей — К-1), не замерены; К-5: Ст К1-1, Ст В1-1, Ст Т3-1, Ст К1-2 (кухня), Ст В1-2, Ст Т3-2 — положение стояка принято проектировщиком (проект ВК дома не передан), не замерено.

Открытые вопросы и конфликты по листу: К-9.

Изменения по листу без подписи: ИЗ-1.

См. лист открытых вопросов (лист 7, записи К-1, К-2, К-4, К-5; лист 8, записи К-7, К-9; лист 9, запись ИЗ-1).

Примечания

1. Привязки выводов даны от чистовых поверхностей стен (облицовка на сторону: санузел гостевой — 24 мм (штукатурка 10 + клей 5 + плитка 9); гостиная-кухня — 24 мм (фартук: штукатурка 10 + клей 5 + плитка 9)); эти же грани — на развёртках и в раскладке плитки. Высоты — от чистого пола помещения.
2. Высоты и межосевые, отмеченные «*», приняты по практике монтажа; до черновой разводки сверить по паспорту выбранного прибора (смеситель, инсталляция, сифон).
3. Горячая вода (Т3) — слева от холодной (В1), если смотреть на прибор. Допуск установки выводов: ±5 мм в группе, ±20 мм у отдельно стоящих.
4. Расчёт систем водоснабжения и канализации и подбор оборудования выполняет проектная организация; лист задаёт места и высоты выводов.
5. Посудомоечная машина Кх3: кран и слив — отдельными выводами в шкафу мойки (не за машиной), до машины ≤ 1500 мм.
6. Прибор Кх2 мойка кухонная, Кх3 посудомоечная машина взят из расстановки мебели (по шкафу с мойкой).
7. Ст К1-1*, Ст В1-1*, Ст Т3-1*, Ст К1-2 (кухня)*, Ст В1-2*, Ст Т3-2* на обмере не показаны: положение принято (исполнитель по плану заказчика), проект ВК дома не передан, не замерено (К-5); положение сверить на объекте до разметки.
8. Стояки в коробах/шахтах не замоноличивать; стояк К1 в коробе — звукоизоляция стояка в коробе без жёсткого контакта с трубой; к арматуре и ревизиям — люк не меньше 300×400.

1000 мм · печать 1:1

Изм.	Кол.уч	Лист	№ док.	Подп.	Дата
Разраб.		Кырлан А.С.			04.11.26
Пров.					
ГИП					
Н. контр.					
Утв.					

ГД-2026-012-АИ

Дом 120 м²

Общая площадь 147,36* м² · * размеры приняты, не замерены (реестр — л. 7–9, К-1)

Дизайн-проект интерьера	Стадия	Лист	Листов
	РП	52	175

План выводов сантехники · 1-й этаж

М 1:40

Кырлан Александр Сергеевич


выпуск 04.11.2026 № 4dfa962484 · стр. 54 из 180

План выводов сантехники · 2-й этаж

Выводы В1, Т3, К1 · привязки от чистовых стен · высоты от чистого пола, мм

ПРЕДВАРИТЕЛЬНО · не для производства работ · открыто пунктов: 11 (реестр — л. 7–9)

Фрагмент 1. Санузел второго этажа (пом. 13)

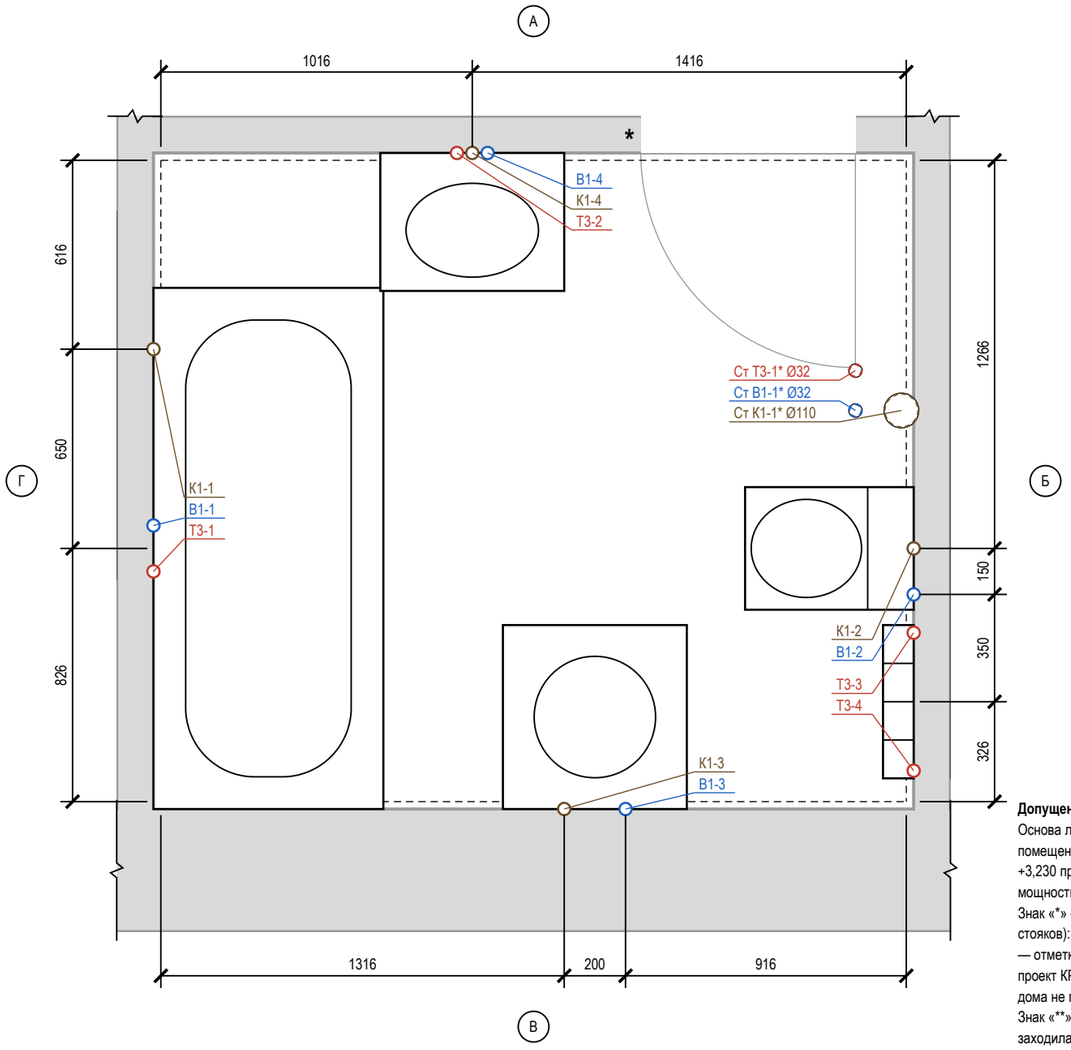

Ведомость привязок выводов

Код	Прибор	Ø	H, мм	Привязка от чист. стен, мм	Прим.
В1-1	См1** ванна	½"	800*	ст. Г: 901 от В	межос. 150
Т3-1	См1** ванна	½"	800*	ст. Г: 751 от В	межос. 150
К1-1	См1** ванна	Ø50	50*	ст. Г: 616 от А	
В1-2	См2** унитаз подвесной	½"	250*	ст. Б: 676 от В	в раме инсталляции
К1-2	См2** унитаз подвесной	Ø110	220*	ст. Б: 826 от В	
В1-3	См3** стиральная машина	½"	600*	ст. В: 916 от Б	кран машины
К1-3	См3** стиральная машина	Ø50	600*	ст. В: 1116 от Б	
В1-4	См4** умывальник	½"	600*	ст. А: 1066 от Г	межос. 100
Т3-2	См4** умывальник	½"	600*	ст. А: 966 от Г	межос. 100
К1-4	См4** умывальник	Ø50	500*	ст. А: 1016 от Г	
Т3-3	См5** полотенцесушитель	½"	1150*	ст. Б: 551 от В	подача, межос. 450; байпас и краны
Т3-4	См5** полотенцесушитель	½"	1150*	ст. Б: 101 от В	обратка

* — высота по практике монтажа; сверить по паспорту прибора

Условные обозначения

- вывод В1 (код — в ведомости привязок)
- вывод Т3 (код — в ведомости привязок)
- вывод К1 (код — в ведомости привязок)
- сантехприбор по расстановке (габарит модели)
- чистовая поверхность стены (от неё привязки)
- стояк «Ст К1-N / Ст В1-N» (ГОСТ 21.601), Ø мм
- * стояк Т3 не на обмере — принят в шахте рядом со Ст В1, сверить
- линия обрыва (граница фрагмента)
- А — обозначение стены А–Г (как на развёртках)

Допущения и предложения на листе

Основа листа: взаимное расположение помещений, контур дома 9600 × 8000 и раскладка этажей подобраны проектировщиком под габариты помещений брифа; обмер и проект АР — задание (К-1); высота потолка 2900 мм — по брифу, не замерена; перекрытие 330 мм и отметка 2-го этажа +3,230 приняты; проект КР — задание (К-2); наружные стены 400 мм, перегородки 120 мм приняты (в брифе толщин нет) (К-1); разрешённая мощность 15 кВт принята по типовым ТУ для частного дома (К-4); подрайон климата не задан — принят не северный (жилые от 2,5 м) (К-7).

Знак «*» — принято, не замерено и не подтверждено (замерить на объекте): К-1: дверь пом. 13 (стена А) — Петли у правого откоса (х 6150, у стояков): открытое полотно стоит вдоль стены Б, вошедший идёт влево к умывальнику и ванне; К-2: отметка чистого пола этажа «2-й этаж» +3,230 — отметка чистого пола 2-го этажа +3,230 принята: высота потолка 2900 по брифу + перекрытие с полом 330 (конструкция перекрытия не задана; проект КР — задание); К-5: Ст К1-1, Ст В1-1, Ст Т3-1, Ст К1-2 (кухня), Ст В1-2, Ст Т3-2 — положение стояка принято проектировщиком (проект ВК дома не передан), не замерено.

Знак «**» — предложение проектировщика, заказчиком не утверждено (согласовать с заказчиком): ИЗ-1: См1 — Было у стены В offset 150 — заходила в полосу 600 мм перед проёмом Д-8 и в зону 750 перед машиной См3; См2 — Было offset 900…1300 — габарит накрывал стояки Ст К1-1 / В1-1 (у 6570…6700); См3 — Было у стены Г offset 300 — пересекалась с умывальником См4 в углу А/Г, люк упирался в раковину; См5 — Было у стены Г offset 1000 — в 2,3 м от стояка ГВС и в полосе перед проёмом; К-9: См4 — Было offset 500…1100 — пересекалась со стиральной машиной См3.

Открытые вопросы и конфликты по листу: К-9.

Изменения по листу без подписи: ИЗ-1.

См. лист открытых вопросов (лист 7, записи К-1, К-2, К-4, К-5; лист 8, записи К-7, К-9; лист 9, запись ИЗ-1).

Примечания

1. Привязки выводов даны от чистовых поверхностей стен (облицовка на сторону: санузел второго этажа — 24 мм (штукатурка 10 + клей 5 + плитка 9)); эти же грани — на развёртках и в раскладке плитки. Высоты — от чистого пола помещения.
2. Высоты и межосевые, отмеченные «*», приняты по практике монтажа; до черновой разводки сверить по паспорту выбранного прибора (смеситель, инсталляция, сифон).
3. Горячая вода (Т3) — слева от холодной (В1), если смотреть на прибор. Допуск установки выводов: ±5 мм в группе, ±20 мм у отдельно стоящих.
4. Расчёт систем водоснабжения и канализации и подбор оборудования выполняет проектная организация; лист задаёт места и высоты выводов.
5. Ст К1-1*, Ст В1-1*, Ст Т3-1*, Ст К1-2 (кухня)*, Ст В1-2*, Ст Т3-2* на обмере не показаны: положение принято (исполнитель по плану заказчика), проект ВК дома не передан, не замерено (К-5); положение сверить на объекте до разметки.
6. Стояки в коробах/шахтах не замоноличивать; стояк К1 в коробе — звукоизоляция стояка в коробе без жёсткого контакта с трубой; к арматуре и ревизиям — люк не меньше 300×400.

1000 мм · печать 1:1

Изм.	Кол.уч	Лист	№ док.	Подп.	Дата
Разраб.		Кырлан А.С.			04.11.26
Пров.					
ГИП					
Н. контр.					
Утв.					

ГД-2026-012-АИ

Дом 120 м²

Общая площадь 147,36* м² · * размеры приняты, не замерены (реестр — л. 7–9, К-1)

Дизайн-проект интерьера

Стадия	Лист	Листов
РП	53	175

План выводов сантехники · 2-й этаж

М 1:20

Кырлан Александр Сергеевич


выпуск 04.11.2026 № 4dfa962484 · стр. 55 из 180

Схема разводки водопровода и канализации · 1-й этаж

Схемы систем В1, Т3, К1 · трассы принципиальные · уклоны в мм на 1 м · план М 1:200, фрагменты М 1:25

ПРЕДВАРИТЕЛЬНО · не для производства работ · открыто пунктов: 11 (реестр — л. 7–9)

План этажа (М 1:200)

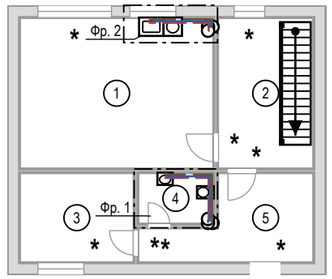

Допущения и предложения на листе

Основа листа: взаимное расположение помещений, контур дома 9600 × 8000 и раскладка этажей подобраны проектировщиком под габариты помещений брифа; обмер и проект АР — задание (К-1); высота потолка 2900 мм — по брифу, не замерена; перекрытие 330 мм и отметка 2-го этажа +3,230 приняты; проект КР — задание (К-2); наружные стены 400 мм, перегородки 120 мм приняты (в брифе толщин нет) (К-1); разрешённая мощность 15 кВт принята по типовым ТУ для частного дома (К-4); подрайон климата не задан — принят не северный (жилые от 2,5 м) (К-7).


Знак «*» — принято, не замерено и не подтверждено (замерить на объекте): К-1: окно пом. 1 (стена А), 2 (А), 3 (В) — окно: место, ширина, высота и подоконник приняты по брифу, стена — по раскладке проектировщика (К-1), не замерены; дверь пом. 1 (стена Б), 3 (Б), 4 (В), 5 (А) — проём: место и ширина приняты проектировщиком по брифу (раскладка этажей — К-1), не замерены; дверь пом. 5 (стена В) — входная дверь: место и ширина проёма приняты проектировщиком по брифу (без плана дома), не замерены; К-5: Ст К1-1, Ст В1-1, Ст Т3-1, Ст К1-2 (кухня), Ст В1-2, Ст Т3-2 — положение стояка принято проектировщиком (проект ВК дома не передан), не замерено.

Открытые вопросы и конфликты по листу: К-5, К-6, К-9.


Изменения по листу без подписи: ИЗ-1.

См. лист открытых вопросов (лист 7, записи К-1, К-2, К-4–К-6; лист 8, записи К-7, К-9; лист 9, запись ИЗ-1).

Фр. 1. Санузел гостевой (М 1:25)

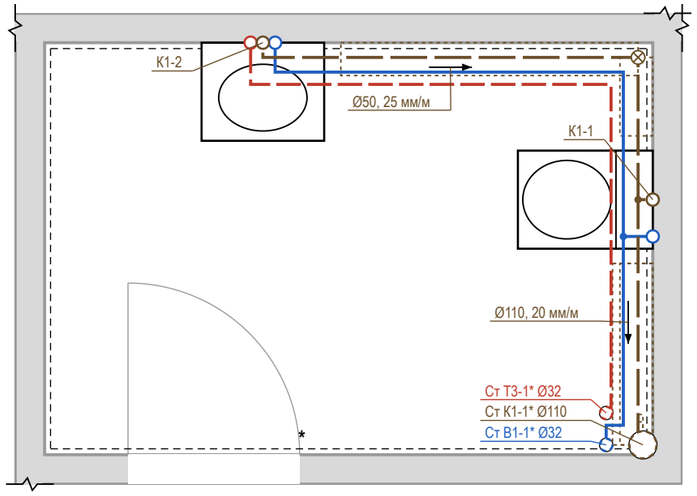

Фр. 2. Гостиная-кухня (М 1:25)

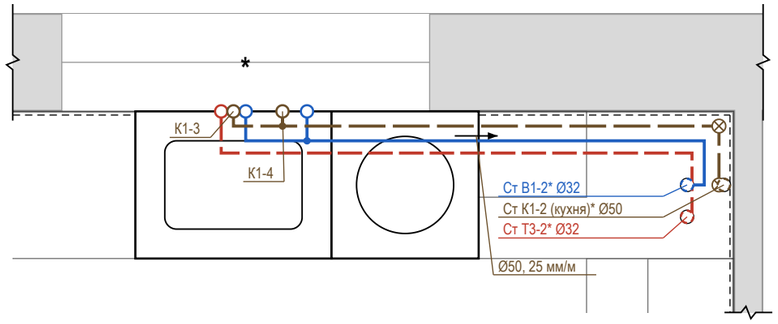

Условные обозначения


- В1 — водопровод хозяйственно-питьевой (ХВС), PP-R Ø20
- Т3 — горячее водоснабжение, подача (ГВС), PP-R Ø20
- К1 — канализация бытовая
- направление уклона К1 / пола: Ø, мм на 1 м
- ревизия (прочистка) К1 — доступ сохранить
- тройник (ответвление к прибору)
- короб К1 над чистым полом (ГКЛВ под плитку)
- вывод В1 (код — в ведомости привязок)
- вывод Т3 (код — в ведомости привязок)
- вывод К1 (код — в ведомости привязок)
- сантехприбор по расстановке (габарит модели)
- стояк «Ст К1-N / Ст В1-N» (ГОСТ 21.601), Ø мм
- * стояк Т3 не на обмере — принят в шахте рядом со Ст В1, сверить
- линия обрыва (граница фрагмента)
- граница фрагмента на плане (Фр. N)

Профиль выпусков К1 (до врезки в стояк)

Выпуск	Прибор	Ø	L, м	i, мм/м	Δh, мм	Прокладка, мм
К1-1	Ст1 унитаз подвесной	Ø110	1,08	20	22	короб 170×140
К1-2	Ст2 умывальник	Ø50	3,19	25	80	короб 160×110
К1-3	Кх2 мойка кухонная	Ø50	2,30	25	58	над полом за приборами
К1-4	Кх3 посудомоечная машина	Ø40	2,10	30	63	над полом за приборами

Короб h×b: h — от чистого пола, b — от чистовой стены. Стяжка 35 мм — лист полов.

Узел ввода В1, Т3 (схема, без масштаба)

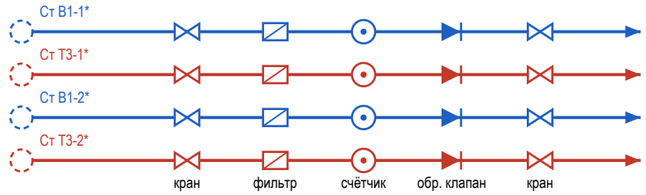

состав узла — по согласованию

⊗ Ст К1-1*, Ст К1-2 (кухня)*: ревизия на стояке — люк в коробе

Примечания

1. Трассы принципиальные, построены от стояков вдоль стен помещений; фактическое положение фиксируется исполнительной схемой с привязками (фото с рулеткой) до закрытия.
2. Уклон К1 не менее 1/d и не более 150 мм/м (СП 30.13330.2020, п. 19.1), приняты практические уклоны; поворот — двумя отводами 45°, ревизия после поворота, доступ сохранить. Стояк К1 в коробе — звукоизоляция стояка в коробе, без жёсткого контакта короба с трубой.
3. Решение по К1: стяжка 35 мм не укрывает трубы (нужно Ø + Δh + 45 мм) — выпуски идут над чистым полом вдоль стен: К1-3, К1-4 — за приборами и в раме инсталляции; К1-1, К1-2 — в коробе ГКЛВ под плитку (размеры в профиле). Короба — на развёртках; отметку низа врезки в стояк замерить до черновых работ.
4. Состав узла ввода В1, Т3 — по согласованию: на схеме типовой узел — кран шаровой, фильтр, счётчик, обратный клапан, кран; состав и места не определены (записи реестра нет). Доступ к арматуре — через люк не меньше 300×400. Водопровод — в штробе стен или в коробах; трубы испытать давлением до закрытия (акт скрытых работ).
5. Расчёт систем, диаметры магистралей и подбор оборудования выполняет проектная организация; положение стояков, выпуск из дома и вентиляция стояков по проекту ВК дома, при его отсутствии — решение владельца с проектной организацией. Арматуру и привязки сверить по паспортам приборов.
6. Ст К1-1*, Ст В1-1*, Ст Т3-1*, Ст К1-2 (кухня)*, Ст В1-2*, Ст Т3-2* на обмере не показаны: положение принято (исполнитель по плану заказчика), проект ВК дома не передан, не замерено (К-5); положение сверить на объекте до разводки.

Изм.	Кол.уч	Лист	№ док.	Подп.	Дата
Разраб.		Кырлан А.С.			04.11.26
Пров.					
ГИП					
Н. контр.					
Утв.					

ГД-2026-012-АИ

Дом 120 м²

Общая площадь 147,36* м² · * размеры приняты, не замерены (реестр — л. 7–9, К-1)

Дизайн-проект интерьера

Стадия	Лист	Листов
РП	54	175

Схема разводки водопровода и канализации · 1-й этаж

М 1:200; 1:25

Кырлан Александр Сергеевич


выпуск 04.11.2026 № 4dfa962484 · стр. 56 из 180

Схема разводки водопровода и канализации · 2-й этаж


Схемы систем В1, Т3, К1 · трассы принципиальные · уклоны в мм на 1 м · план М 1:200, фрагменты М 1:25

ПРЕДВАРИТЕЛЬНО · не для производства работ · открыто пунктов: 11 (реестр — л. 7–9)

План этажа (М 1:200)

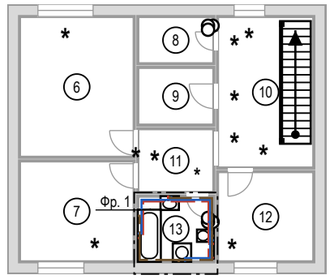

Фр. 1. Санузел второго этажа (М 1:25)

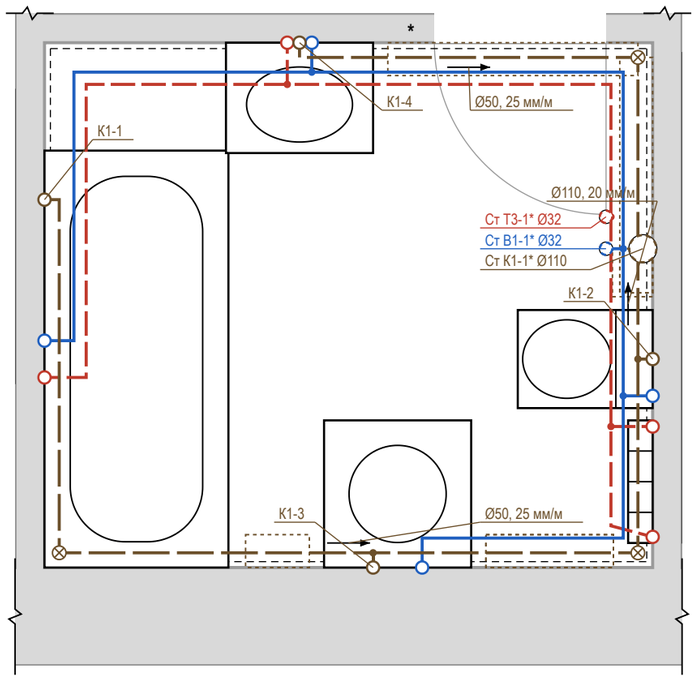

Допущения и предложения на листе. Основа листа: взаимное расположение помещений, контур дома 9600 × 8000 и раскладка этажей подобраны проектировщиком под габариты помещений брифа; обмер и проект АР — задание (К-1); высота потолка 2900 мм — по брифу, не замерена; перекрытие 330 мм и отметка 2-го этажа +3,230 приняты; проект КР — задание (К-2); наружные стены 400 мм, перегородки 120 мм приняты (в брифе толщин нет) (К-1); разрешённая мощность 15 кВт принята по типовым ТУ для частного дома (К-4); подрайон климата не задан — принят не северный (жилые от 2,5 м) (К-7). Знак «*» — принято, не замерено и не подтверждено (замерить на объекте): К-2: отметка чистого пола этажа «2-й этаж» +3,230 — отметка чистого пола 2-го этажа +3,230 принята: высота потолка 2900 по брифу + перекрытие с полом 330 (конструкция перекрытия не задана; проект КР — задание); К-5: Ст К1-1, Ст В1-1, Ст Т3-1, Ст К1-2 (кухня), Ст В1-2, Ст Т3-2 — положение стояка принято проектировщиком (проект ВК дома не передан), не замерено. Знак «**» — предложение проектировщика, заказчиком не утверждено (согласовать с заказчиком): ИЗ-1: См1 — Было у стены В offset 150 — заходила в полосу 600 мм перед проёмом Д-8 и в зону 750 перед машиной См3; См2 — Было offset 900…1300 — габарит накрывал стояки Ст К1-1 / В1-1 (у 6570…6700); См3 — Было у стены Г offset 300 — пересекалась с умывальником См4 в углу А/Г, люк упирался в раковину; К-9: См4 — Было offset 500…1100 — пересекалась со стиральной машиной См3. См. лист открытых вопросов (лист 7, записи К-1, К-2, К-4–К-6; лист 8, записи К-7, К-9; лист 9, запись ИЗ-1); по листу — К-5, К-6, К-9, ИЗ-1.

Условные обозначения


- В1 — водопровод хозяйственно-питьевой (ХВС), PP-R Ø20
- Т3 — горячее водоснабжение, подача (ГВС), PP-R Ø20
- К1 — канализация бытовая
- направление уклона К1 / пола: Ø, мм на 1 м
- ⊗ ревизия (прочистка) К1 — доступ сохранить
- • тройник (ответвление к прибору)
- короб К1 над чистым полом (ГКЛВ под плитку)
- ○ вывод В1 (код — в ведомости привязок)
- ○ вывод Т3 (код — в ведомости привязок)
- ○ вывод К1 (код — в ведомости привязок)
- сантехприбор по расстановке (габарит модели)
- ○ стояк «Ст К1-N / Ст В1-N» (ГОСТ 21.601), Ø мм
- * стояк Т3 не на обмере — принят в шахте рядом со Ст В1, сверить
- линия обрыва (граница фрагмента)
- граница фрагмента на плане (Фр. N)

Профиль выпусков К1 (до врезки в стояк)

Выпуск	Прибор	Ø	L, м	i, мм/м	Δh, мм	Прокладка, мм
К1-2	См2** унитаз подвесной	Ø110	0,53	20	11	короб 160×140
К1-1	См1** ванна	Ø50	5,12	25	128	короб 210×110
К1-3	См3** стиральная машина	Ø50	2,40	25	60	короб 140×110
К1-4	См4** умывальник	Ø50	2,24	25	56	под проёмом Д-8: короба нет; К-9

Короб h×b: h — от чистого пола, b — от чистовой стены. Стяжка 35 мм — лист полов.

Узел ввода В1, Т3 (схема, без масштаба)

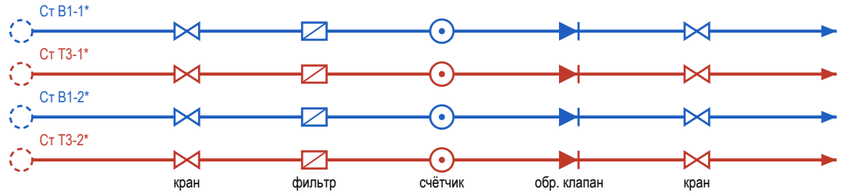

состав узла — по согласованию

⊗ Ст К1-1*, Ст К1-2 (кухня)*: ревизия на стояке — люк в коробе

Примечания

1. Трассы принципиальные, построены от стояков вдоль стен помещений; фактическое положение фиксируется исполнительной схемой с привязками (фото с рулеткой) до закрытия.
2. Уклон К1 не менее 1/d и не более 150 мм/м (СП 30.13330.2020, п. 19.1), приняты практические уклоны; поворот — двумя отводами 45°, ревизия после поворота, доступ сохранить. Стояк К1 в коробе — звукоизоляция стояка в коробе, без жёсткого контакта короба с трубой.
3. Решение по К1: стяжка 35 мм не укрывает трубы (нужно Ø + Δh + 45 мм) — выпуски идут над чистым полом вдоль стен; К1-2, К1-1, К1-3 — в коробе ГКЛВ под плитку (размеры в профиле). Короба — на развёртках; отметку низа врезки в стояк замерить до черновых работ.
4. К1-4 (См4** умывальник): трасса К1 до Ст К1-1* — под проёмом Д-8, короб там не поставить: прибор ближе к стояку, выпуск в полу с подъёмом пола или насосная установка (КНС) — решение К-9; до решения не выполнять.
5. Отводы К1-1 (5,1 м) длиннее 4 м без вентиляции — у прибора воздушный клапан Ø50 в доступном месте (за люком или в тумбе) либо вентилируемый отвод (EN 12056-2, табл. 4); предложение проектировщика, подбор — проектная организация.
6. Состав узла ввода В1, Т3 — по согласованию: на схеме типовой узел — кран шаровой, фильтр, счётчик, обратный клапан, кран; состав и места не определены (записи реестра нет). Доступ к арматуре — через люк не меньше 300×400. Водопровод — в штробе стен или в коробах; трубы испытать давлением до закрытия (акт скрытых работ).
7. Расчёт систем, диаметры магистралей и подбор оборудования выполняет проектная организация; положение стояков, выпуск из дома и вентиляция стояков по проекту ВК дома, при его отсутствии — решение владельца с проектной организацией. Арматуру и привязки сверить по паспортам приборов.
8. Ст К1-1*, Ст В1-1*, Ст Т3-1*, Ст К1-2 (кухня)*, Ст В1-2*, Ст Т3-2* на обмере не показаны: положение принято (исполнитель по плану заказчика), проект ВК дома не передан, не замерено (К-5); положение сверить на объекте до разводки.

Изм.	Кол.уч	Лист	№ док.	Подп.	Дата
Разраб.		Кырлан А.С.			04.11.26
Пров.					
ГИП					
Н. контр.					
Утв.					

ГД-2026-012-АИ

Дом 120 м²

Общая площадь 147,36* м² · * размеры приняты, не замерены (реестр — л. 7–9, К-1)

Дизайн-проект интерьера

Стадия	Лист	Листов
РП	55	175

Схема разводки водопровода и канализации · 2-й этаж
М 1:200; 1:25

Кырлан Александр Сергеевич


выпуск 04.11.2026 № 4dfa962484 · стр. 57 из 180

Аксонометрическая схема В1 (холодное водоснабжение)

аксонометрия · диаметры, уклоны, отметки, стояки и приборы · трассы принципиальные

Схема В1 (М 1:50; по вертикали и горизонтали один масштаб, глубина — ×0,5 под 45°)

ПРЕДВАРИТЕЛЬНО · не для производства работ · открыто пунктов: 11 (реестр — л. 7–9)

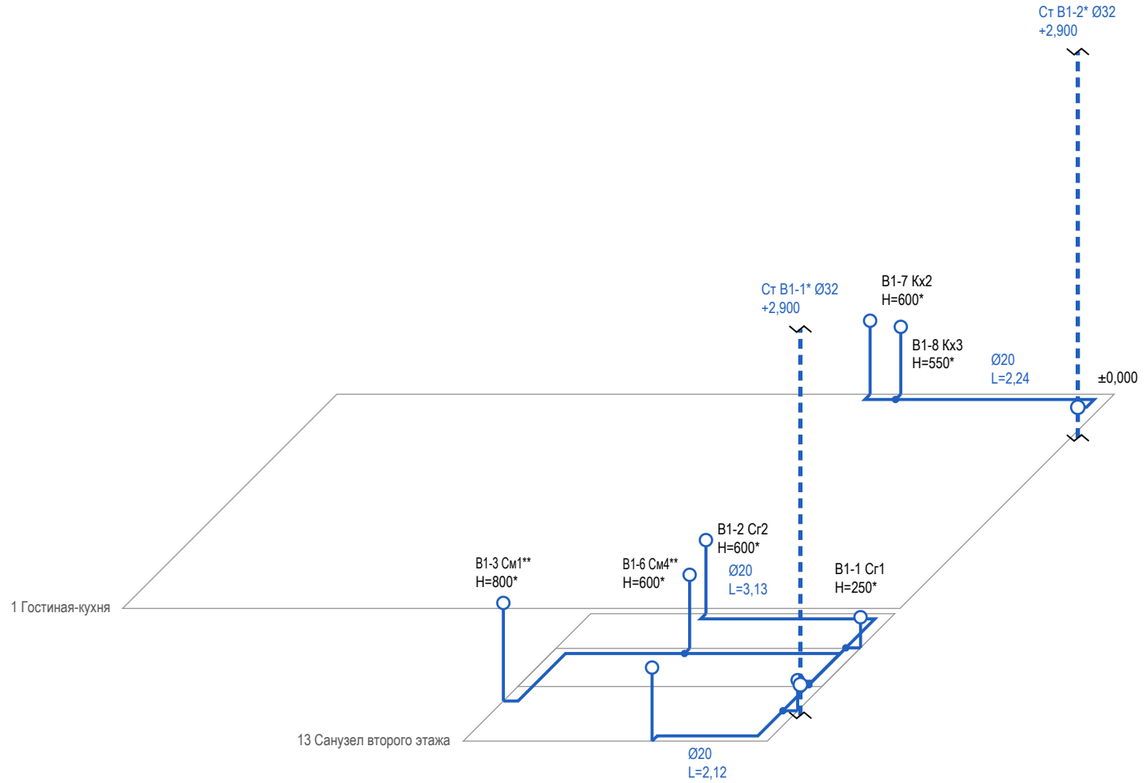

Условные обозначения

- В1 — водопровод хозяйственно-питьевой (ХВС), PP-R Ø20
- вывод В1 (код — в ведомости привязок)
- стояк «Ст К1-N / Ст В1-N» (ГОСТ 21.601), Ø мм
- стояк в плане (на отметке пола); вертикаль — стояк по высоте, разрыв — перекрытие
- тройник (ответвление к прибору)
- кран шаровой
- * стояк Т3 не на обмере — принят в шахте рядом со Ст В1, сверить

Допущения и предложения на листе

Основа листа: взаимное расположение помещений, контур дома 9600 × 8000 и раскладка этажей подобраны проектировщиком под габариты помещений брифа; обмер и проект АР — задание (К-1); высота потолка 2900 мм — по брифу, не замерена; перекрытие 330 мм и отметка 2-го этажа +3,230 приняты; проект КР — задание (К-2); наружные стены 400 мм, перегородки 120 мм приняты (в брифе толщин нет) (К-1); разрешённая мощность 15 кВт принята по типовым ТУ для частного дома (К-4); подрайон климата не задан — принят не северный (жилые от 2,5 м) (К-7).

Знак «*» — принято, не замерено и не подтверждено (замерить на объекте): К-5: Ст В1-1, Ст В1-2, Ст К1-1, Ст Т3-1, Ст К1-2 (кухня), Ст Т3-2 — положение стояка принято проектировщиком (проект ВК дома не передан), не замерено.

Знак «**» — предложение проектировщика, заказчиком не утверждено (согласовать с заказчиком): ИЗ-1: См1 — Было у стены В offset 150 — заходила в полосу 600 мм перед проёмом Д-8 и в зону 750 перед машиной См3; К-9: См4 — Было offset 500…1100 — пересекалась со стиральной машиной См3.

См. лист открытых вопросов (лист 7, записи К-1, К-2, К-4, К-5; лист 8, записи К-7, К-9; лист 9, запись ИЗ-1).

Примечания

1. Схема В1 построена по тем же трассам, что план разводки: положение в плане сохранено, глубина — в масштабе ×0,5. Трассы принципиальные; фактическое положение фиксируется исполнительной схемой до закрытия.
2. Высоты Н — от чистого пола помещения, мм. Отметка прокладки магистрали В1 (в стяжке, в стене или по полу) в данных не задана: участки показаны на уровне пола условно (записи реестра нет).
3. * — высота вывода принята по практике монтажа; сверить по паспорту прибора.
4. Узел ввода В1 (кран, фильтр, счётчик, обратный клапан, кран) — на схеме разводки; состав узла ввода — по согласованию. Кран шаровой — на первом участке от стояка.
5. Ст В1-1*, Ст В1-2* на обмере не показаны: положение принято (исполнитель по плану заказчика), проект ВК дома не передан, не замерено (К-5); положение сверить на объекте до разводки.
6. Трубы испытать давлением до закрытия (акт скрытых работ, опрессовка по СП 73.13330.2016).
7. Диаметры, высоты выводов и места кранов — по паспортам выбранных приборов и расчёту проектной организации.
8. Расчёт систем, диаметры магистралей и подбор оборудования выполняет проектная организация.

1000 мм · печать 1:1

Изм.	Кол.уч	Лист	№ док.	Подп.	Дата
Разраб.		Кырлан А.С.			04.11.26
Пров.					
ГИП					
Н. контр.					
Утв.					

ГД-2026-012-АИ

Дом 120 м²

Общая площадь 147,36* м² · * размеры приняты, не замерены (реестр — л. 7–9, К-1)

Дизайн-проект интерьера

Стадия	Лист	Листов
РП	56	175

Аксонометрическая схема В1 (холодное водоснабжение)

М 1:50


Кырлан Александр Сергеевич

выпуск 04.11.2026 № 4dfa962484 · стр. 58 из 180

Аксонометрическая схема Т3 (горячее водоснабжение)

аксонометрия · диаметры, уклоны, отметки, стояки и приборы · трассы принципиальные

Схема Т3 (М 1:50; по вертикали и горизонтали один масштаб, глубина — ×0,5 под 45°)

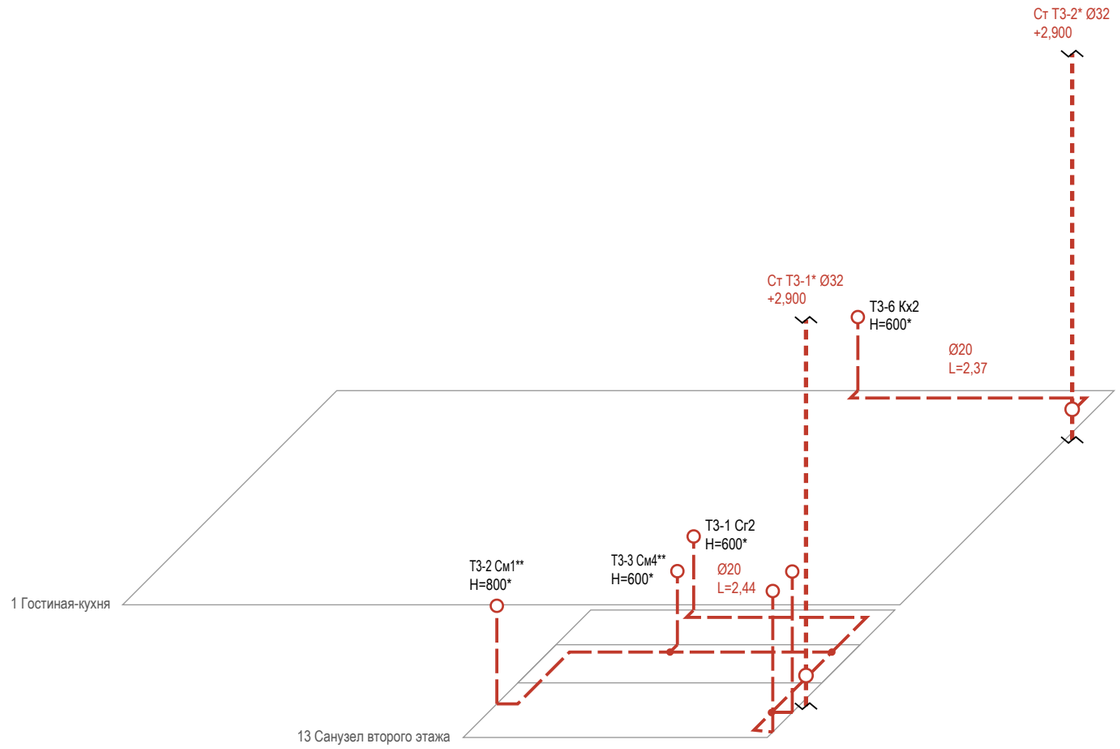

Допущения и предложения на листе

Основа листа: взаимное расположение помещений, контур дома 9600 × 8000 и раскладка этажей подобраны проектировщиком под габариты помещений брифа; обмер и проект АР — задание (К-1); высота потолка 2900 мм — по брифу, не замерена; перекрытие 330 мм и отметка 2-го этажа +3,230 приняты; проект КР — задание (К-2); наружные стены 400 мм, перегородки 120 мм приняты (в брифе толщин нет) (К-1); разрешённая мощность 15 кВт принята по типовым ТУ для частного дома (К-4); подрайон климата не задан — принят не северный (жилые от 2,5 м) (К-7).

Знак «*» — принято, не замерено и не подтверждено (замерить на объекте): К-5: Ст Т3-1, Ст Т3-2, Ст К1-1, Ст В1-1, Ст К1-2 (кухня), Ст В1-2 — положение стояка принято проектировщиком (проект ВК дома не передан), не замерено.

Знак «**» — предложение проектировщика, заказчиком не утверждено (согласовать с заказчиком): ИЗ-1: См1 — Было у стены В offset 150 — заходила в полосу 600 мм перед проёмом Д-8 и в зону 750 перед машиной См3; К-9: См4 — Было offset 500…1100 — пересекалась со стиральной машиной См3.

См. лист открытых вопросов (лист 7, записи К-1, К-2, К-4, К-5; лист 8, записи К-7, К-9; лист 9, запись ИЗ-1).

Примечания

1. Схема Т3 построена по тем же трассам, что план разводки: положение в плане сохранено, глубина — в масштабе ×0,5. Трассы принципиальные; фактическое положение фиксируется исполнительной схемой до закрытия.
2. Высоты Н — от чистого пола помещения, мм. Отметка прокладки магистрали Т3 (в стяжке, в стене или по полу) в данных не задана: участки показаны на уровне пола условно (записи реестра нет).
3. * — высота вывода принята по практике монтажа; сверить по паспорту прибора.
4. Узел ввода Т3 (кран, фильтр, счётчик, обратный клапан, кран) — на схеме разводки; состав узла ввода — по согласованию. Кран шаровой — на первом участке от стояка.
5. Циркуляция ГВС в данных не задана — циркуляционного трубопровода на схеме нет (записи реестра нет).
6. Ст Т3-1*, Ст Т3-2* на обмере не показаны: положение принято (исполнитель по плану заказчика), проект ВК дома не передан, не замерено (К-5); положение сверить на объекте до разводки.
7. Трубы испытать давлением до закрытия (акт скрытых работ, опрессовка по СП 73.13330.2016).
8. Диаметры, высоты выводов и места кранов — по паспортам выбранных приборов и расчёту проектной организации.
9. Расчёт систем, диаметры магистралей и подбор оборудования выполняет проектная организация.

1000 мм · печать 1:1

ПРЕДВАРИТЕЛЬНО · не для производства работ · открыто пунктов: 11 (реестр — л. 7–9)

Условные обозначения

- Т3 — горячее водоснабжение, подача (ГВС), PP-R Ø20
- вывод Т3 (код — в ведомости привязок)
- стояк «Ст К1-N / Ст В1-N» (ГОСТ 21.601), Ø мм
- стояк в плане (на отметке пола); вертикаль — стояк по высоте, разрыв — перекрытие
- тройник (ответвление к прибору)
- кран шаровой
- * стояк Т3 не на обмере — принят в шахте рядом со Ст В1, сверить

Изм.	Кол.уч	Лист	№ док.	Подп.	Дата
Разраб.		Кырлан А.С.			04.11.26
Пров.					
ГИП					
Н. контр.					
Утв.					

ГД-2026-012-АИ

Дом 120 м²

Общая площадь 147,36* м² · * размеры приняты, не замерены (реестр — л. 7–9, К-1)

Дизайн-проект интерьера

Стадия	Лист	Листов
РП	57	175

Аксонометрическая схема Т3 (горячее водоснабжение)

М 1:50

Кырлан Александр Сергеевич


выпуск 04.11.2026 № 4dfa962484 · стр. 59 из 180

Аксонометрическая схема К1 (канализация)

аксонометрия · диаметры, уклоны, отметки, стояки и приборы · трассы принципиальные

Схема К1 (М 1:50; по вертикали и горизонтали один масштаб, глубина — ×0,5 под 45°)

ПРЕДВАРИТЕЛЬНО · не для производства работ · открыто пунктов: 11 (реестр — л. 7–9)

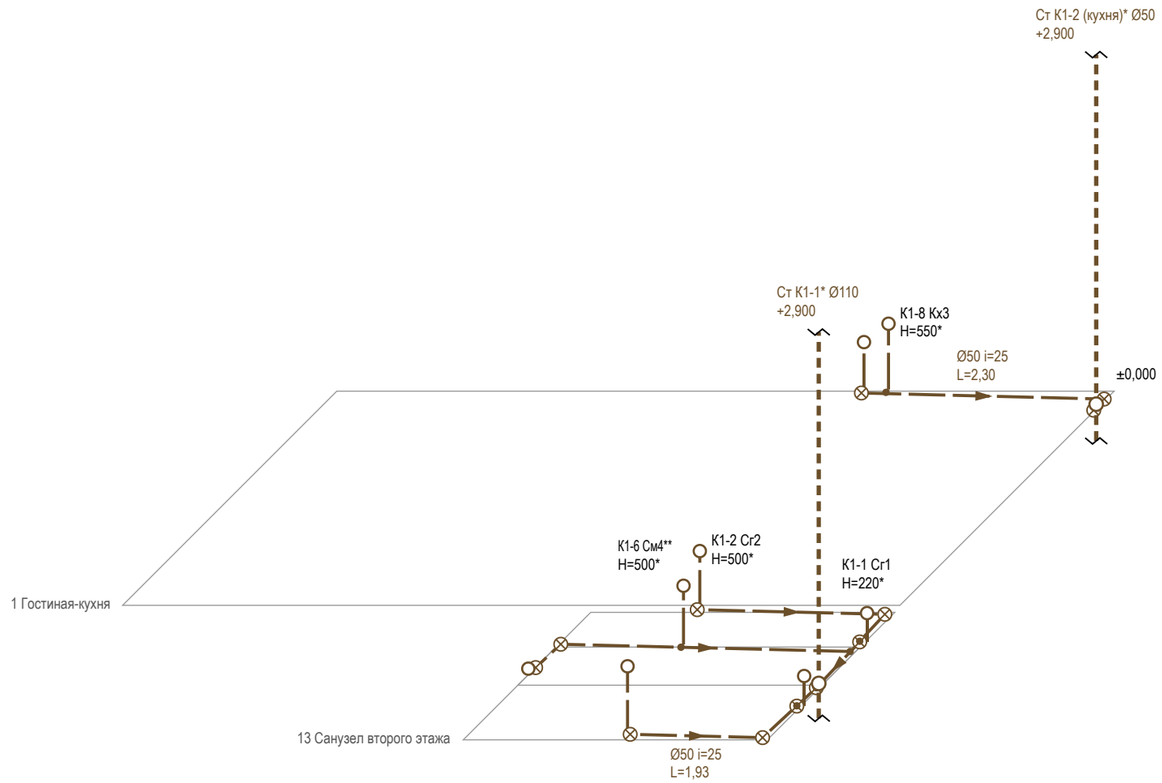

Условные обозначения

- К1 — канализация бытовая
- вывод К1 (код — в ведомости привязок)
- стояк «Ст К1-N / Ст В1-N» (ГОСТ 21.601), Ø мм
- стояк в плане (на отметке пола); вертикаль — стояк по высоте, разрыв — перекрытие
- направление уклона К1 / пола: Ø, мм на 1 м
- ревизия (прочистка) К1 — доступ сохранить
- тройник (ответвление к прибору)
- * стояк Т3 не на обмере — принят в шахте рядом со Ст В1, сверить

Допущения и предложения на листе

Основа листа: взаимное расположение помещений, контур дома 9600 × 8000 и раскладка этажей подобраны проектировщиком под габариты помещений брифа; обмер и проект АР — задание (К-1); высота потолка 2900 мм — по брифу, не замерена; перекрытие 330 мм и отметка 2-го этажа +3,230 приняты; проект КР — задание (К-2); наружные стены 400 мм, перегородки 120 мм приняты (в брифе толщин нет) (К-1); разрешённая мощность 15 кВт принята по типовым ТУ для частного дома (К-4); подрайон климата не задан — принят не северный (жилые от 2,5 м) (К-7).

Знак «*» — принято, не замерено и не подтверждено (замерить на объекте): К-5: Ст К1-1, Ст К1-2 (кухня), Ст В1-1, Ст Т3-1, Ст В1-2, Ст Т3-2 — положение стояка принято проектировщиком (проект ВК дома не передан), не замерено.

Знак «**» — предложение проектировщика, заказчиком не утверждено (согласовать с заказчиком): К-9: См4 — Было offset 500…1100 — пересекалась со стиральной машиной См3.

См. лист открытых вопросов (лист 7, записи К-1, К-2, К-4, К-5; лист 8, записи К-7, К-9).

Примечания

1. Схема К1 построена по тем же трассам, что план разводки: положение в плане сохранено, глубина — в масштабе ×0,5. Трассы принципиальные; фактическое положение фиксируется исполнительной схемой до закрытия.
2. Отметки — от плиты перекрытия: низ трубы у врезки в стояк — отметка из данных выпуска, к прибору труба поднимается на уклон i, мм/м (уклон не менее 1/d и не более 150 мм/м, СП 30.13330.2020, п. 19.1); чистый пол — выше плиты на стяжку (высота пирога пола). Высота выпуска прибора H — от чистого пола.
3. * — высота вывода принята по практике монтажа; сверить по паспорту прибора.
4. Ревизия — на повороте и в начале участка; стояк К1 в коробе с люком — звукоизоляция стояка в коробе; поворот — двумя отводами 45°.
5. Ст К1-1*, Ст К1-2 (кухня)* на обмере не показаны: положение принято (исполнитель по плану заказчика), проект ВК дома не передан, не замерено (К-5); положение сверить на объекте до разводки.
6. Трубы испытать давлением до закрытия (акт скрытых работ, опрессовка по СП 73.13330.2016).
7. Диаметры, высоты выводов и места кранов — по паспортам выбранных приборов и расчёту проектной организации.
8. Расчёт систем, диаметры магистралей и подбор оборудования выполняет проектная организация.

1000 мм · печать 1:1

Изм.	Кол.уч	Лист	№ док.	Подп.	Дата
Разраб.		Кырлан А.С.			04.11.26
Пров.					
ГИП					
Н. контр.					
Утв.					

ГД-2026-012-АИ

Дом 120 м²

Общая площадь 147,36* м² · * размеры приняты, не замерены (реестр — л. 7–9, К-1)

Дизайн-проект интерьера

Стадия	Лист	Листов
РП	58	175

Аксонометрическая схема К1 (канализация)

М 1:50

Кырлан Александр Сергеевич


выпуск 04.11.2026 № 4dfa962484 · стр. 60 из 180

Развёртки мокрых зон: выводы ВК. Гостиная-кухня

пом. 1 · выводы В1, Т3, К1 на стенах · высоты от чистого пола, привязки от чистовых углов, мм

ПРЕДВАРИТЕЛЬНО · не для производства работ · открыто пунктов: 11 (реестр — л. 7–9)

Стена А (М 1:25)

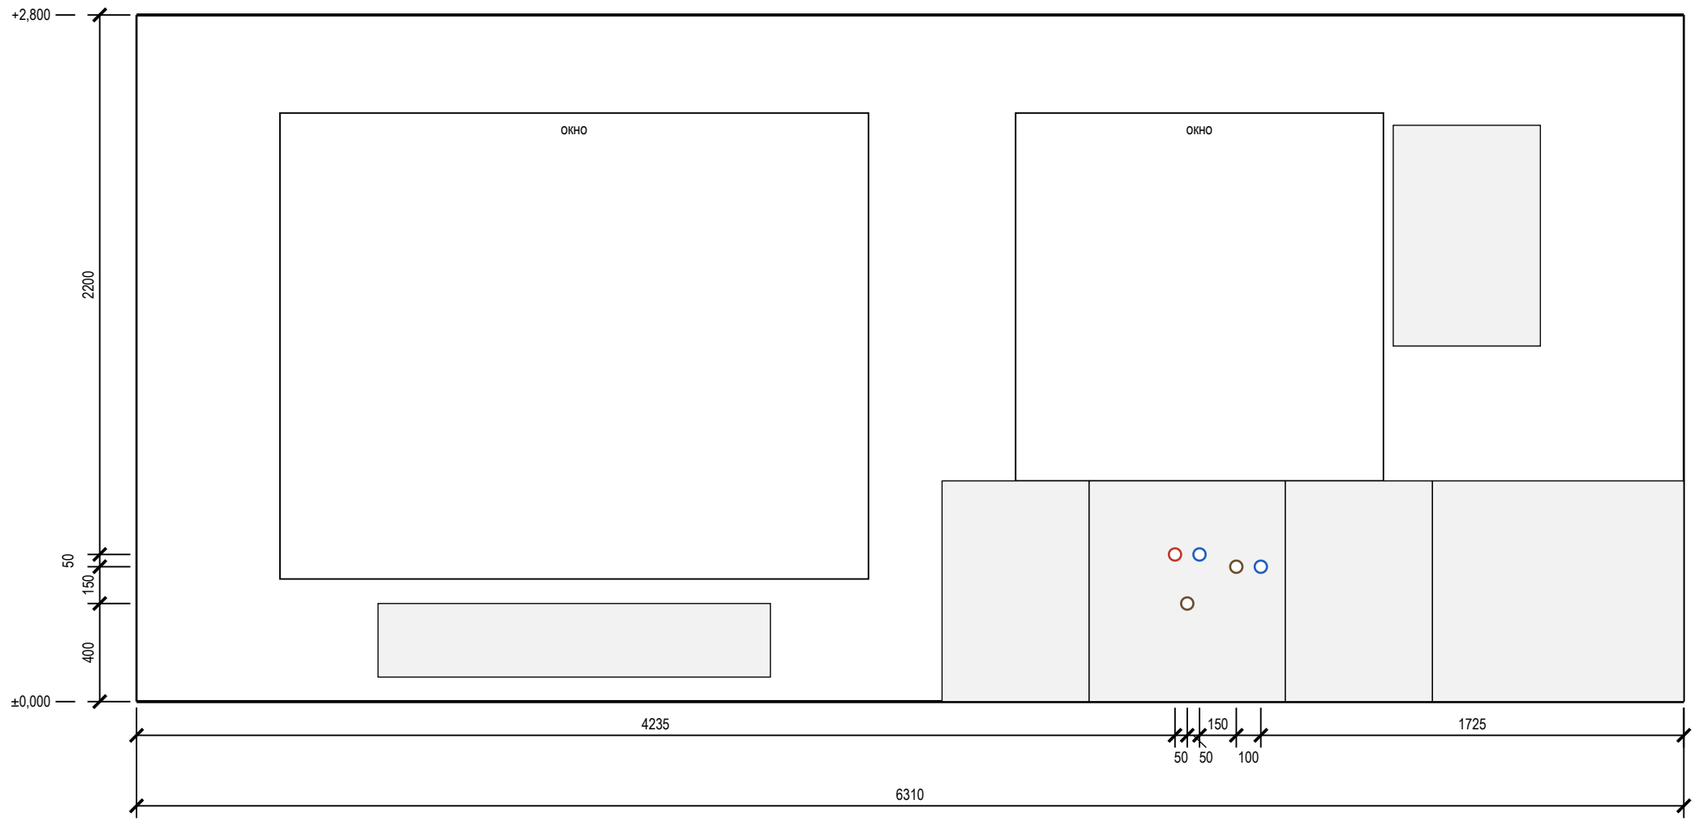

Допущения и предложения на листе

Основа листа: взаимное расположение помещений, контур дома 9600 × 8000 и раскладка этажей подобраны проектировщиком под габариты помещений брифа; обмер и проект АР — задание (К-1); высота потолка 2900 мм — по брифу, не замерена; перекрытие 330 мм и отметка 2-го этажа +3,230 приняты; проект КР — задание (К-2); наружные стены 400 мм, перегородки 120 мм приняты (в брифе толщин нет) (К-1); разрешённая мощность 15 кВт принята по типовым ТУ для частного дома (К-4); подрайон климата не задан — принят не северный (жилые от 2,5 м) (К-7).

Знак «*» — принято, не замерено и не подтверждено (замерить на объекте): К-1: окно пом. 1 (стена А) — окно: место, ширина, высота и подоконник приняты по брифу, стена — по раскладке проектировщика (К-1), не замерены; дверь пом. 1 (стена Б) — проём: место и ширина приняты проектировщиком по брифу (раскладка этажей — К-1), не замерены; К-5: Ст К1-2 (кухня), Ст В1-2, Ст Т3-2 — положение стояка принято проектировщиком (проект ВК дома не передан), не замерено.

См. лист открытых вопросов (лист 7, записи К-1, К-2, К-4, К-5; лист 8, запись К-7).

Ведомость привязок выводов (от чистого пола и угла)

Код	Прибор	Ø	H, мм	Привязка, мм
В1-7	Кх2 мойка кухонная	½"	600*	ст. А: 4335 от лев. угла
Т3-6	Кх2 мойка кухонная	½"	600*	ст. А: 4235 от лев. угла
К1-7	Кх2 мойка кухонная	Ø50	400*	ст. А: 4285 от лев. угла
В1-8	Кх3 посудомоечная машина	½"	550*	ст. А: 4585 от лев. угла
К1-8	Кх3 посудомоечная машина	Ø40	550*	ст. А: 4485 от лев. угла

Условные обозначения

- вывод В1 (код — в ведомости привязок)
- вывод Т3 (код — в ведомости привязок)
- вывод К1 (код — в ведомости привязок)
- сантехприбор по расстановке (габарит модели)
- дверной проём; окно — сплошной контур

Примечания

1. Габариты и высоты приборов, межосевые смесители и места кранов — по паспортам выбранных приборов, сверяются до разметки стен.
2. Высоты H — от чистого пола помещения, мм; отметка чистого пола и потолка — у левого края вида (от ±0,000 объекта). Привязки — от левого чистового угла вида (облицовка стен вычтена), как на развёртках стен.
3. * — высота принята по практике монтажа: в данных прибора её нет; до разметки стен сверить по паспорту выбранного прибора (смеситель, инсталляция, сифон).
4. Стояки в помещении: Ст К1-2 (кухня)* Ø50, Ст В1-2* Ø32, Ст Т3-2* Ø32 — положение на плане выводов; выводы подключаются к ним по схеме разводки.
5. Ревизионные люки к арматуре и ревизиям в данных не заданы: место и размер не определены (записи реестра нет).
6. Мойка, ПММ и фильтр — выводы в шкафу мойки; диаметры и положение сифона и кранов сверить по паспортам приборов и чертежам модуля.
7. Часть подписей выводов не уместилась у знака: коды и высоты — в ведомости привязок.
8. Расчёт систем водоснабжения и канализации и подбор оборудования выполняет проектная организация; лист задаёт места и высоты выводов.

1000 мм · печать 1:1

Изм.	Кол.уч	Лист	№ док.	Подп.	Дата
Разраб.		Кырлан А.С.			04.11.26
Пров.					
ГИП					
Н. контр.					
Утв.					

ГД-2026-012-АИ

Дом 120 м²

Общая площадь 147,36* м² · * размеры приняты, не замерены (реестр — л. 7–9, К-1)

Дизайн-проект интерьера	Стадия	Лист	Листов
	РП	59	175

Развёртки мокрых зон: выводы ВК. Гостиная-кухня

М 1:25

Кырлан Александр Сергеевич


выпуск 04.11.2026 № 4dfa962484 · стр. 61 из 180

Развёртки мокрых зон: выводы ВК. Санузел гостевой


ПРЕДВАРИТЕЛЬНО · не для производства работ · открыто пунктов: 11 (реестр — л. 7–9)

пом. 4 · выводы В1, Т3, К1 на стенах · высоты от чистого пола, привязки от чистовых углов, мм

Стена А (М 1:20)

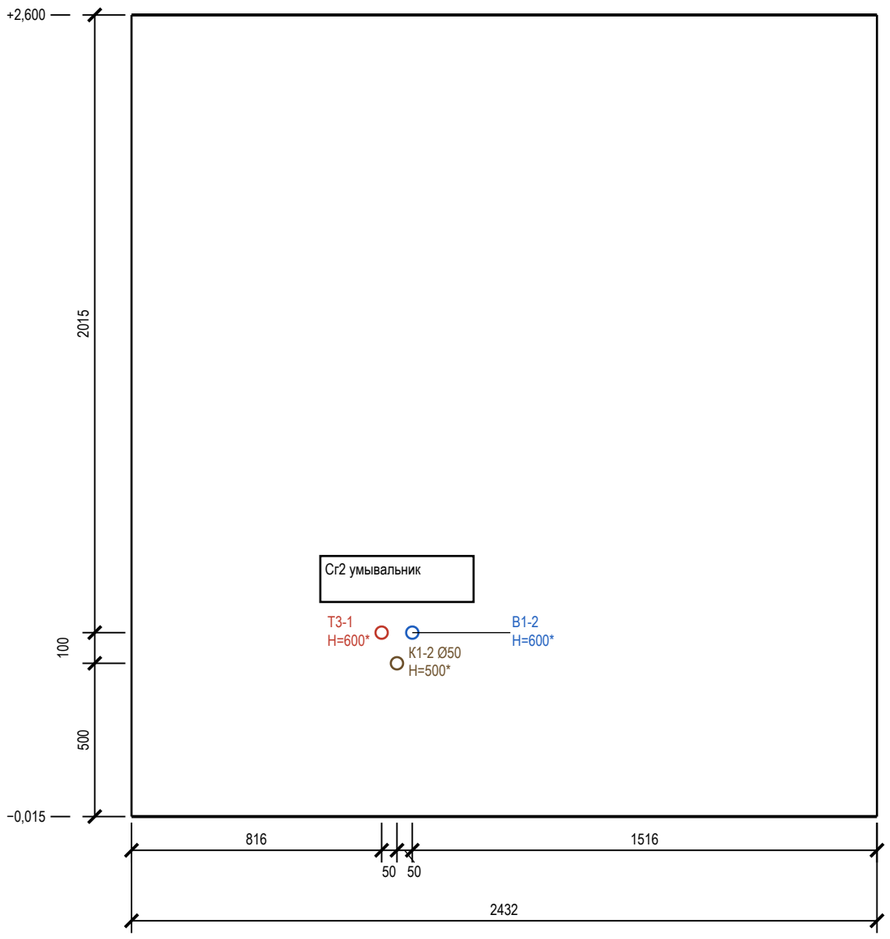

Стена Б (М 1:20)

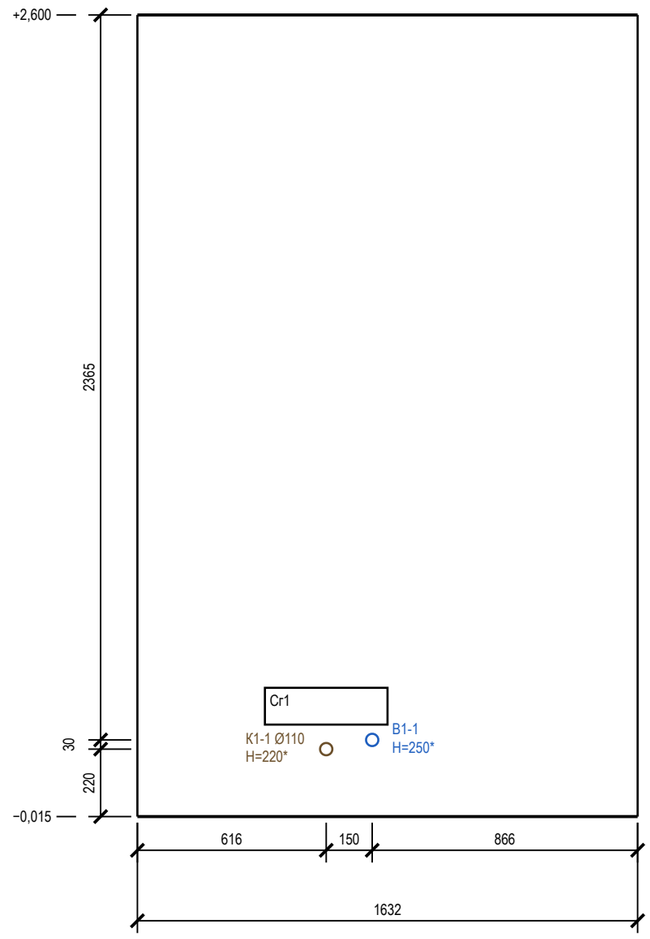

Допущения и предложения на листе

Основа листа: взаимное расположение помещений, контур дома 9600 × 8000 и раскладка этажей подобраны проектировщиком под габариты помещений брифа; обмер и проект АР — задание (К-1); высота потолка 2900 мм — по брифу, не замерена; перекрытие 330 мм и отметка 2-го этажа +3,230 приняты; проект КР — задание (К-2); наружные стены 400 мм, перегородки 120 мм приняты (в брифе толщин нет) (К-1); разрешённая мощность 15 кВт принята по типовым ТУ для частного дома (К-4); подрайон климата не задан — принят не северный (жилые от 2,5 м) (К-7).

Знак «*» — принято, не замерено и не подтверждено (замерить на объекте): К-5: Ст К1-1, Ст В1-1, Ст Т3-1 — положение стояка принято проектировщиком (проект ВК дома не передан), не замерено.

См. лист открытых вопросов (лист 7, записи К-1, К-2, К-4, К-5; лист 8, запись К-7).

Ведомость привязок выводов (от чистого пола и угла)

Код	Прибор	Ø	Н, мм	Привязка, мм
В1-2	Cr2 умывальник	½"	600*	ст. А: 916 от лев. угла
Т3-1	Cr2 умывальник	½"	600*	ст. А: 816 от лев. угла
К1-2	Cr2 умывальник	Ø50	500*	ст. А: 866 от лев. угла

Ведомость привязок (продолжение)

Код	Прибор	Ø	Н, мм	Привязка, мм
В1-1	Cr1 унитаз подвесной	½"	250*	ст. Б: 766 от лев. угла
К1-1	Cr1 унитаз подвесной	Ø110	220*	ст. Б: 616 от лев. угла

Условные обозначения

- вывод В1 (код — в ведомости привязок)
- вывод Т3 (код — в ведомости привязок)
- вывод К1 (код — в ведомости привязок)
- сантехприбор по расстановке (габарит модели)
- дверной проём; окно — сплошной контур

Примечания

1. Габариты и высоты приборов, межосевые смесителей и места кранов — по паспортам выбранных приборов, сверяются до разметки стен.
2. Высоты Н — от чистого пола помещения, мм; отметка чистого пола и потолка — у левого края вида (от ±0,000 объекта). Привязки — от левого чистового угла вида (облицовка стен вычтена), как на развёртках стен.
3. * — высота принята по практике монтажа: в данных прибора её нет; до разметки стен сверить по паспорту выбранного прибора (смеситель, инсталляция, сифон).
4. Стояки в помещении: Ст К1-1* Ø110, Ст В1-1* Ø32, Ст Т3-1* Ø32 — положение на плане выводов; выводы подключаются к ним по схеме разводки.
5. Ревизионные люки к арматуре и ревизиям в данных не заданы: место и размер не определены (записи реестра нет).
6. Расчёт систем водоснабжения и канализации и подбор оборудования выполняет проектная организация; лист задаёт места и высоты выводов.

1000 мм · печать 1:1

Изм.	Кол.уч	Лист	№ док.	Подп.	Дата				
Разраб.		Кырлан А.С.			04.11.26	ГД-2026-012-АИ			
Пров.						Дом 120 м²			
ГИП						Общая площадь 147,36* м² · * размеры приняты, не замерены (реестр — л. 7–9, К-1)			
						Дизайн-проект интерьера	Стадия	Лист	Листов
Н. контр.							РП	60	175
Утв.						Развёртки мокрых зон: выводы ВК. Санузел гостевой М 1:20	Кырлан Александр Сергеевич		


выпуск 04.11.2026 № 4dfa962484 · стр. 62 из 180

Развёртки мокрых зон: выводы ВК. Санузел второго этажа (лист 1 из 2)


пом. 13 · выводы В1, Т3, К1 на стенах · высоты от чистого пола, привязки от чистовых углов, мм

ПРЕДВАРИТЕЛЬНО · не для производства работ · открыто пунктов: 11 (реестр — л. 7–9)

Стена А (М 1:20)

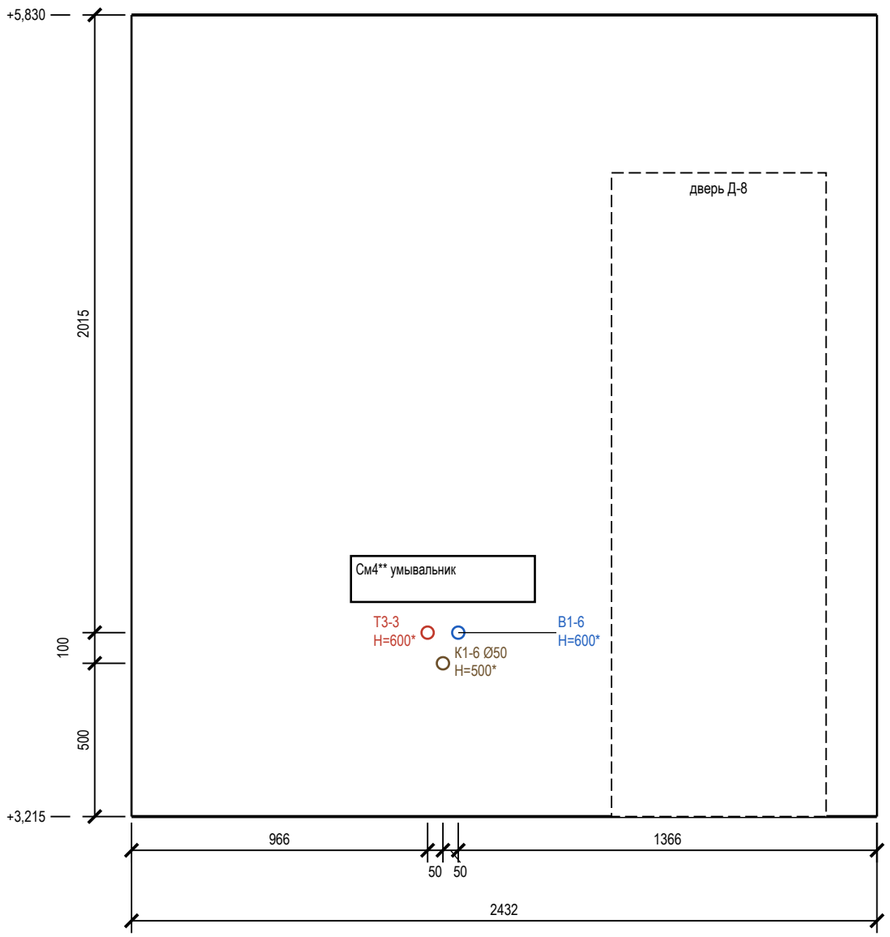

Стена Б (М 1:20)

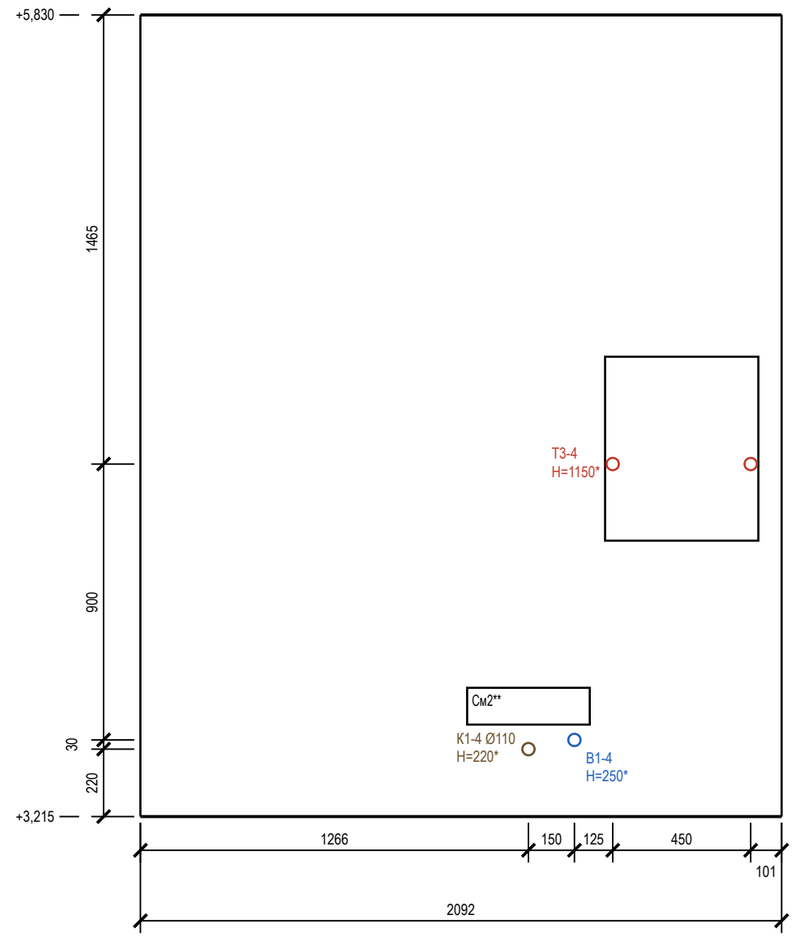

Допущения и предложения на листе

Основа листа: взаимное расположение помещений, контур дома 9600 × 8000 и раскладка этажей подобраны проектировщиком под габариты помещений брифа; обмер и проект АР — задание (К-1); высота потолка 2900 мм — по брифу, не замерена; перекрытие 330 мм и отметка 2-го этажа +3,230 приняты; проект КР — задание (К-2); наружные стены 400 мм, перегородки 120 мм приняты (в брифе толщин нет) (К-1); разрешённая мощность 15 кВт принята по типовым ТУ для частного дома (К-4); подрайон климата не задан — принят не северный (жилые от 2,5 м) (К-7).

Знак «*» — принято, не замерено и не подтверждено (замерить на объекте): К-1: дверь пом. 13 (стена А) — Петли у правого откоса (х 6150, у стояков): открытое полотно стоит вдоль стены Б, вошедший идёт влево к умывальнику и ванне.

Знак «**» — предложение проектировщика, заказчиком не утверждено (согласовать с заказчиком): ИЗ-1: См2 — Было offset 900…1300 — габарит накрывал стояки Ст К1-1 / В1-1 (у 6570…6700); См5 — Было у стены Г offset 1000 — в 2,3 м от стояка ГВС и в полосе перед проёмом; К-9: См4 — Было offset 500…1100 — пересекалась со стиральной машиной См3.

См. лист открытых вопросов (лист 7, записи К-1, К-2, К-4; лист 8, записи К-7, К-9; лист 9, запись ИЗ-1).

Ведомость привязок выводов (от чистого пола и угла)

Код	Прибор	Ø	H, мм	Привязка, мм
В1-6	См4** умывальник	½"	600*	ст. А: 1066 от лев. угла
Т3-3	См4** умывальник	½"	600*	ст. А: 966 от лев. угла
К1-6	См4** умывальник	Ø50	500*	ст. А: 1016 от лев. угла
В1-4	См2** унитаз подвесной	½"	250*	ст. Б: 1416 от лев. угла

Ведомость привязок (продолжение)

Код	Прибор	Ø	H, мм	Привязка, мм
К1-4	См2** унитаз подвесной	Ø110	220*	ст. Б: 1266 от лев. угла
Т3-4	См5** полотенцесушитель	½"	1150*	ст. Б: 1541 от лев. угла
Т3-5	См5** полотенцесушитель	½"	1150*	ст. Б: 1991 от лев. угла

Условные обозначения

- вывод В1 (код — в ведомости привязок)
- вывод Т3 (код — в ведомости привязок)
- вывод К1 (код — в ведомости привязок)
- сантехприбор по расстановке (габарит модели)
- дверной проём; окно — сплошной контур

Примечания

1. Габариты и высоты приборов, межосевые смесителей и места кранов — по паспортам выбранных приборов, сверяются до разметки стен.
2. Высоты H — от чистого пола помещения, мм; отметка чистого пола и потолка — у левого края вида (от ±0,000 объекта). Привязки — от левого чистового угла вида (облицовка стен вычтена), как на развёртках стен.
3. * — высота принята по практике монтажа: в данных прибора её нет; до разметки стен сверить по паспорту выбранного прибора (смеситель, инсталляция, сифон).
4. Ревизионные люки к арматуре и ревизиям в данных не заданы: место и размер не определены (записи реестра нет).
5. Часть подписей выводов не уместилась у знака: коды и высоты — в ведомости привязок.
6. Помещение «Санузел второго этажа» — 2 листа: стены 1) А, Б; 2) В, Г.
7. Расчёт систем водоснабжения и канализации и подбор оборудования выполняет проектная организация; лист задаёт места и высоты выводов.

1000 мм · печать 1:1

Изм.	Кол.уч	Лист	№ док.	Подп.	Дата
Разраб.		Кырлан А.С.			04.11.26
Пров.					
ГИП					
Н. контр.					
Утв.					

ГД-2026-012-АИ

Дом 120 м²

Общая площадь 147,36* м² · * размеры приняты, не замерены (реестр — л. 7–9, К-1)

Дизайн-проект интерьера	Стадия	Лист	Листов
	РП	61	175

Развёртки мокрых зон: выводы ВК. Санузел второго этажа (лист 1 из 2)

М 1:20

Кырлан Александр Сергеевич


выпуск 04.11.2026 № 4dfa962484 · стр. 63 из 180

Развёртки мокрых зон: выводы ВК. Санузел второго этажа (лист 2 из 2)


пом. 13 · выводы В1, Т3, К1 на стенах · высоты от чистого пола, привязки от чистовых углов, мм

ПРЕДВАРИТЕЛЬНО · не для производства работ · открыто пунктов: 11 (реестр — л. 7–9)

Стена В (М 1:20)

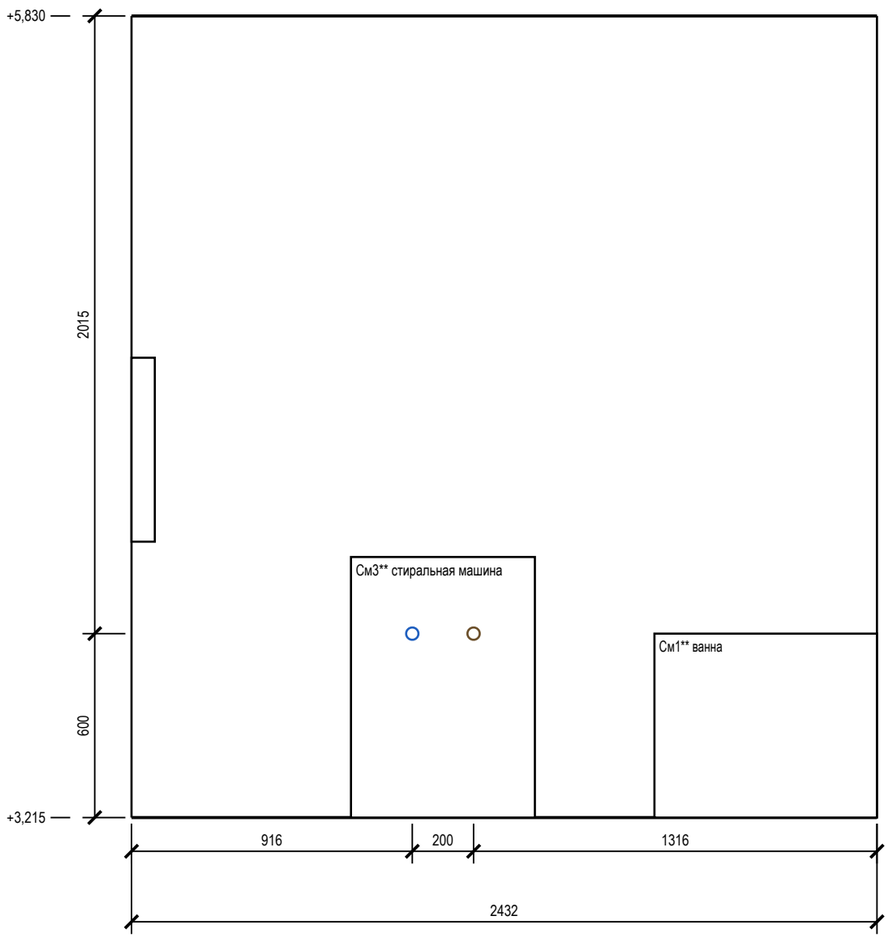

Стена Г (М 1:20)

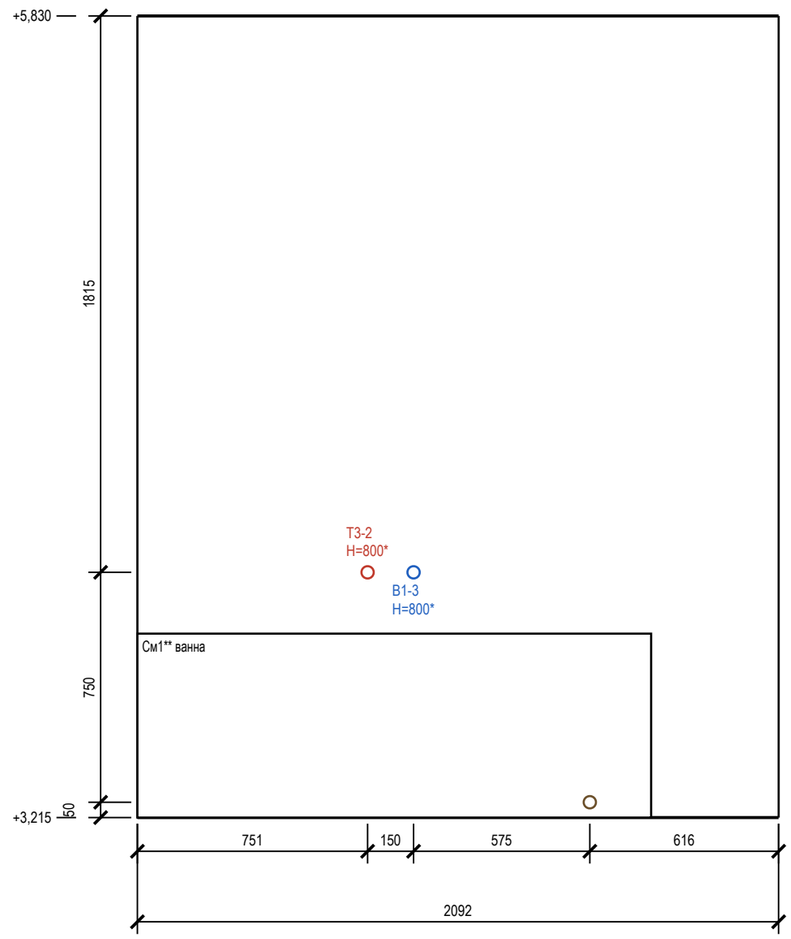

Допущения и предложения на листе

Основа листа: взаимное расположение помещений, контур дома 9600 × 8000 и раскладка этажей подобраны проектировщиком под габариты помещений брифа; обмер и проект АР — задание (К-1); высота потолка 2900 мм — по брифу, не замерена; перекрытие 330 мм и отметка 2-го этажа +3,230 приняты; проект КР — задание (К-2); наружные стены 400 мм, перегородки 120 мм приняты (в брифе толщин нет) (К-1); разрешённая мощность 15 кВт принята по типовым ТУ для частного дома (К-4); подрайон климата не задан — принят не северный (жилые от 2,5 м) (К-7).

Знак «**» — предложение проектировщика, заказчиком не утверждено (согласовать с заказчиком): ИЗ-1: См1 — Было у стены В offset 150 — заходила в полосу 600 мм перед проёмом Д-8 и в зону 750 перед машиной См3; См3 — Было у стены Г offset 300 — пересекалась с умывальником См4 в углу А/Г, люк упирался в раковину.

См. лист открытых вопросов (лист 7, записи К-1, К-2, К-4; лист 8, запись К-7; лист 9, запись ИЗ-1).

Ведомость привязок выводов (от чистого пола и угла)

Код	Прибор	Ø	H, мм	Привязка, мм
В1-5	См3** стиральная машина	½"	600*	ст. В: 916 от лев. угла
К1-5	См3** стиральная машина	Ø50	600*	ст. В: 1116 от лев. угла
В1-3	См1** ванна	½"	800*	ст. Г: 901 от лев. угла

Ведомость привязок (продолжение)

Код	Прибор	Ø	H, мм	Привязка, мм
Т3-2	См1** ванна	½"	800*	ст. Г: 751 от лев. угла
К1-3	См1** ванна	Ø50	50*	ст. Г: 1476 от лев. угла

Условные обозначения

- вывод В1 (код — в ведомости привязок)
- вывод Т3 (код — в ведомости привязок)
- вывод К1 (код — в ведомости привязок)
- сантехприбор по расстановке (габарит модели)
- дверной проём; окно — сплошной контур

Примечания

1. Габариты и высоты приборов, межосевые смесителей и места кранов — по паспортам выбранных приборов, сверяются до разметки стен.
2. Высоты H — от чистого пола помещения, мм; отметка чистого пола и потолка — у левого края вида (от ±0,000 объекта). Привязки — от левого чистового угла вида (облицовка стен вычтена), как на развёртках стен.
3. * — высота принята по практике монтажа: в данных прибора её нет; до разметки стен сверить по паспорту выбранного прибора (смеситель, инсталляция, сифон).
4. Ревизионные люки к арматуре и ревизиям в данных не заданы: место и размер не определены (записи реестра нет).
5. Часть подписей выводов не уместилась у знака: коды и высоты — в ведомости привязок.
6. Помещение «Санузел второго этажа» — 2 листа: стены 1) А, Б; 2) В, Г.
7. Расчёт систем водоснабжения и канализации и подбор оборудования выполняет проектная организация; лист задаёт места и высоты выводов.

1000 мм · печать 1:1

Изм.	Кол.уч	Лист	№ док.	Подп.	Дата
Разраб.		Кырлан А.С.			04.11.26
Пров.					
ГИП					
Н. контр.					
Утв.					

ГД-2026-012-АИ

Дом 120 м²

Общая площадь 147,36* м² · * размеры приняты, не замерены (реестр — л. 7–9, К-1)

Дизайн-проект интерьера

Стадия	Лист	Листов
РП	62	175

Развёртки мокрых зон: выводы ВК. Санузел второго этажа (лист 2 из 2)

М 1:20

Кырлан Александр Сергеевич

выпуск 04.11.2026 № 4dfa962484 · стр. 64 из 180

Спецификация сантехнического оборудования

Форма 1 ГОСТ 21.110-2013 · ГД-2026-012-АИ-ВК.СО · приборы, арматура, трубопроводы

ПРЕДВАРИТЕЛЬНО · не для производства работ · открыто пунктов: 11 (реестр — л. 7–9)

Поз.	Наименование и техническая характеристика	Тип, марка, обозначение документа	Код продукции	Поставщик	Ед. изм.	Кол.	Масса 1 ед., кг	Примечание
	Санитарные приборы							
1	Ванна встраиваемая акриловая 1700×750 мм, с каркасом, экраном и отверстием слив-перелив	аналог		выбор заказчика	шт	1		См1**
2	Унитаз подвесной безободковый, с сиденьем микролифт, крепёж и звукоизолирующая прокладка	Jacob Delafon Struktura EDF102-00		выбор заказчика	шт	2		Сг1, См2**
3	Инсталляция для подвесного унитаза: рама высотой 1120 мм, бачок, клавиша смыва (ось клавиши 1050 мм от чистого пола)	аналог		выбор заказчика	шт	2		Сг1, См2**; короб ГКЛВ
4	Умывальник подвесной 500×400 мм, с отверстием под смеситель и переливом	аналог		выбор заказчика	шт	1		Сг2
5	Умывальник подвесной 600×450 мм, с отверстием под смеситель и переливом	аналог		выбор заказчика	шт	1		См4**
6	Мойка кухонная врезная / подстольная, с переливом, ориентир 700×480 мм — в модуле Кх2 шириной 800 мм, вырез по шаблону модели	аналог		с кухонной мебелью	шт	1		Кх2
7	Полотенцесушитель водяной (ГВС), с байпасом и кранами	аналог		выбор заказчика	шт	1		См5**
	Смесители, сифоны и арматура приборов							
8	Смеситель для ванны настенный однорычажный, межосевое 150 мм, с душевым набором (лейка, шланг, держатель)	аналог		выбор заказчика	шт	1		См1**
9	Смеситель для умывальника однорычажный, с донным клапаном	аналог		выбор заказчика	шт	2		Сг2, См4**
10	Смеситель кухонный однорычажный, высокий излив	аналог		выбор заказчика	шт	1		Кх2
11	Обвязка ванны слив-перелив Ø40/50 с сифоном	аналог		выбор заказчика	шт	1		См1**
12	Сифон для умывальника бутылочный Ø32/40–50, с гофрой к выпуску	аналог		выбор заказчика	шт	2		Сг2, См4**
13	Сифон для мойки Ø40/50	аналог		выбор заказчика	шт	1		Кх2
14	Сифон для посудомоечной машины с обратным клапаном, на выводе слива Ø40	аналог		выбор заказчика	шт	1		Кх3
15	Сифон для стиральной машины встраиваемый в стену Ø50, с обратным клапаном	аналог		выбор заказчика	шт	1		См3**
16	Кран угловой ½"×½" с гибкой подводкой 40 см (умывальники, мойка)	аналог		выбор заказчика	шт	6		по 2 на прибор
17	Кран шаровой угловой ½"×¾" для подключения стиральной и посудомоечной машины	аналог		выбор заказчика	шт	2		См3**, Кх3
18	Узел подключения полотенцесушителя: байпас Ду20, краны шаровые ½" ×2	аналог		выбор заказчика	шт	1		
	Трубопроводы							
19	Труба полипропиленовая PP-R PN20 Ø20×3,4 (В1)	ГОСТ 32415-2013		выбор заказчика	м	18,5	0,17	12,2 + 4,3 + 10 %
20	Труба PP-R, армированная стекловолокном, PN20 Ø20×2,8 (Т3)	ГОСТ 32415-2013		выбор заказчика	м	17,5	0,15	10,7 + 4,9 + 10 %
21	Труба канализационная ПП Ø40 (К1)	ГОСТ 32414-2013		выбор заказчика	м	1		0,1 + 0,6 + 10 %
22	Труба канализационная ПП Ø50 (К1)	ГОСТ 32414-2013		выбор заказчика	м	13		9,5 + 2,0 + 10 %
23	Труба канализационная ПП Ø110 (К1)	ГОСТ 32414-2013		выбор заказчика	м	2,5		1,6 + 0,4 + 10 %
	Фасонные части и выводы							
24	Отвод канализационный ПП 45° Ø50	ГОСТ 32414-2013		выбор заказчика	шт	18		2 шт. на поворот
25	Отвод канализационный ПП 45° Ø110	ГОСТ 32414-2013		выбор заказчика	шт	6		2 шт. на поворот
26	Тройник канализационный ПП 45° (врезки ветвей)	ГОСТ 32414-2013		выбор заказчика	шт	7		
27	Ревизия канализационная ПП (после поворота трассы)	ГОСТ 32414-2013		выбор заказчика	шт	6		доступ сохранить
28	Фитинги PP-R Ø20: тройники, угольники 90° (ветви и повороты В1, Т3)	ГОСТ 32415-2013		выбор заказчика	шт	35		
29	Водорозетка PP-R Ø20×½" настенная, с креплением	ГОСТ 32415-2013		выбор заказчика	шт	14		коды — лист выводов
	Узлы ввода, люки, короба							
30	Кран шаровой латунный Ду15 PN16 (отключение ввода)	аналог		выбор заказчика	шт	4		Ст В1-1*, Ст Т3-1*, Ст В1-2*, Ст Т3-2*
31	Фильтр сетчатый косой Ду15	аналог		выбор заказчика	шт	4		
32	Счётчик воды крыльчатый Ду15 (ХВ, ГВ), с поверкой	аналог		выбор заказчика	шт	4		пломба УК
33	Клапан обратный Ду15	аналог		выбор заказчика	шт	4		
34	Люк ревизионный нажимной под плитку 300×400 мм	аналог		выбор заказчика	шт	2		к стоякам и арматуре
35	Звукоизоляция стояка К1 в коробе: рулонный звукоизоляционный материал ≥ 10 мм, обмотка стояка на высоту этажа	аналог		выбор заказчика	м	5,8		Ст К1-1*, Ст К1-2 (кухня)
36	Короб К1 над полом: профиль ПН/ПС, ГКЛВ 12,5 мм под плитку	аналог		выбор заказчика	м	9,5		сечение — лист разводки

Примечания

1. Форма 1 ГОСТ 21.110-2013, ширины граф изменены по п. 4.1. «Аналог» — аналог по характеристикам: модели внести до черновых работ, привязки выводов сверить по паспортам.
2. Бытовая техника не входит (показана арматура подключения), мойка — в комплекте кухни (марка — модуля кухни, как у столяра). Длины труб — трасса листа разводки + подъёмы + 10 %.
3. Стояк К1 в коробе — звукоизоляция стояка в коробе без жёсткого контакта короба с трубой. Стояки со «*» (Ст К1-1*, Ст В1-1*, Ст Т3-1*, Ст К1-2 (кухня)*, Ст В1-2*, Ст Т3-2*) приняты — положение и число узлов ввода сверить на объекте.
4. Расчёт систем водоснабжения и канализации, диаметры магистралей и подбор оборудования выполняет проектная организация.

Допущения и предложения на листе

Основа листа: взаимное расположение помещений, контур дома 9600 × 8000 и раскладка этажей подобраны проектировщиком под габариты помещений брифа; обмер и проект АР — задание (К-1); высота потолка 2900 мм — по брифу, не замерена; перекрытие 330 мм и отметка 2-го этажа +3,230 приняты; проект КР — задание (К-2); наружные стены 400 мм, перегородки 120 мм приняты (в брифе толщин нет) (К-1); разрешённая мощность 15 кВт принята по типовым ТУ для частного дома (К-4); подрайон климата не задан — принят не северный (жилые от 2,5 м) (К-7).
Знак «*» — принято, не замерено и не подтверждено (замерить на объекте): К-5: Ст К1-1, Ст В1-1, Ст Т3-1, Ст К1-2 (кухня), Ст В1-2, Ст Т3-2 — положение стояка принято проектировщиком (проект ВК дома не передан), не замерено.
Знак «**» — предложение проектировщика, заказчиком не утверждено (согласовать с заказчиком): ИЗ-1: См1 — Было у стены В offset 150 — заходила в полосу 600 мм перед проёмом Д-8 и в зону 750 перед машиной См3; См2 — Было offset 900…1300 — габарит накрывал стояки Ст К1-1 / В1-1 (у 6570…6700); См3 — Было у стены Г offset 300 — пересекалась с умывальником См4 в углу А/Г, люк упирался в раковину; См5 — Было у стены Г offset 1000 — в 2,3 м от стояка ГВС и в полосе перед проёмом; К-9: См4 — Было offset 500…1100 — пересекалась со стиральной машиной См3.
См. лист открытых вопросов (лист 7, записи К-1, К-2, К-4, К-5; лист 8, записи К-7, К-9; лист 9, запись ИЗ-1).

Изм.	Кол.уч	Лист	№ док.	Подп.	Дата	ГД-2026-012-АИ		
						Дом 120 м²		
						Общая площадь 147,36* м² · * размеры приняты, не замерены (реестр — л. 7–9, К-1)		
Разраб.		Кырлан А.С.			04.11.26	Дизайн-проект интерьера	Стадия: РП	Лист: 63 / Листов: 175
Пров.								
ГИП								
Н. контр.						Спецификация сантехнического оборудования — М б/м	Кырлан Александр Сергеевич	
Утв.								

Техническое задание на подбор светильников

Параметры для подбора: светильники, ленты и блоки питания, сценарии помещений со светорегуляторами · б/м

Параметры светильников для подбора

Поз.	Марки	Наименование	Установка	Кол.	P, Вт	Σ P, Вт	Ф, лм	Тц, K	Ra	Угол, °	IP	Дим.	Слой	Группа	Пом.
1	Св31–Св40	Встраиваемый точечный	в ГКЛ, корпус ≤ 70 мм	10	12	120	1000	3000	90	—	20	да	общий	L12	1
2	Св41	Лента светодиодная 24 В	в карнизе короба, профиль с рассеивателем	20,5 м	9,6/м	196,4	900/м	2700	90	—	20	да	акцентный	L13	1
3	Св42**, Св43**, Св44**	Подвесной	подвес, низ H=1450	3	9	27	800	3000	90	—	20	да	общий	L14	1
4	Св45–Св48	Встраиваемый точечный	в ГКЛ, корпус ≤ 70 мм	4	10	40	900	3000	90	—	20	да	общий	L15	1
5	Св49**	Линейный настенный	под верхними шкафами, H=1440	1	18	18	1500	3000	90	—	20	да	рабочий	L16	1
6	Св26–Св29, Св53, Св54, Св82–Св85, Св93, Св94	Встраиваемый точечный	в ГКЛ, корпус ≤ 70 мм	12	7	84	600	3000	90	—	20	—	общий	L10, L84	2, 5, 10, 11
7	Св80	Подвесной	подвес	1	12	12	1100	3000	90	—	20	—	общий	L80	2
8	Св17–Св22	Встраиваемый точечный	в ГКЛ, корпус ≤ 70 мм	6	14	84	1400	2700	90	—	20	—	общий	L7	3
9	Св23	Лента светодиодная 24 В	в нише уровня, профиль с рассеивателем	5,7 м	9,6/м	54,7	900/м	2700	90	—	20	да	акцентный	L8	3
10	Св50	Встраиваемый точечный	в ГКЛ, корпус ≤ 70 мм	1	7	7	600	3000	90	—	44	—	общий	L17	4
11	Св12–Св14, Св51	Встраиваемый точечный	в ГКЛ, корпус ≤ 70 мм	4	6	24	500	3000	90	—	44	—	общий	L4, L17	4, 13
12	Св15**, Св52**	Настенный светильник над зеркалом, драйвер встроен	над зеркалом, H=1900	2	8	16	600	3000	90	—	44	—	рабочий	L5, L18	4, 13
13	Св30**	Лента светодиодная 24 В	на поверхности, профиль с рассеивателем, датчик движения	1,8 м	4,8/м	8,6	150/м	2700	90	—	20	нет	ночной	L11	5
14	Св1–Св8	Встраиваемый точечный	в ГКЛ, корпус ≤ 70 мм	8	12	96	1000	2700	90	—	20	—	общий	L1	6
15	Св9	Лента светодиодная 24 В	в нише уровня, профиль с рассеивателем	4,5 м	9,6/м	43,1	900/м	2700	90	—	20	да	акцентный	L2	6
16	Св10, Св11, Св24, Св102	Настенный (бра)	на стене, H=1500	4	6	24	400	2700	90	60	20	—	рабочий	L3, L9	6, 7, 12
17	Св86–Св91, Св95–Св100	Встраиваемый точечный	в ГКЛ, корпус ≤ 70 мм	12	11	132	1100	2700	90	—	20	—	общий	L7	7, 12
18	Св92	Лента светодиодная 24 В	в карнизе короба, профиль с рассеивателем	12 м	9,6/м	114,8	900/м	2700	90	—	20	да	акцентный	L8	7
19	Св16	Потолочный накладной	на потолке, засветка стены	1	10	10	900	3000	90	—	20	—	общий	L6	8
20	Св25	Потолочный накладной	на потолке	1	9	9	600	3000	90	—	20	—	общий	L3	9
21	Св101	Лента светодиодная 24 В	в карнизе короба, профиль с рассеивателем	10,1 м	9,6/м	96,6	900/м	2700	90	—	20	да	акцентный	L8	12
		Итого		**70 шт + 54,5 м**		**1217,3**									

LED-ленты, линейные светильники и блоки питания

Марка	Пом.	L, м	U, В	Вт/м	Σ P, Вт	БП	P БП, Вт	Загр., %	Питание	Доступ к БП
Св41	1	20,5	24	9,6	196,4	БП4	300	65	с двух концов	люк 300×300 в коробе потолка ПТ1
Св49**	1	3	24	—	18	БП5**	60	30	встроенный ввод	в пенале Кх10, верх, съёмная панель
Св23	3	5,7	24	9,6	54,7	БП2	200	27	с двух концов	люк 300×300 в нише фигуры потолка ПТ4
Св30**	5	1,8	24	4,8	8,6	БП3	20	43	с одного конца	в шкафу Пх1, верхняя полка
Св9	6	4,5	24	9,6	43,1	БП1	200	22	с двух концов	люк 300×300 в нише фигуры потолка ПТ6
Св92	7	12	24	9,6	114,8	БП6	200	57	с двух концов	люк 300×300 в коробе потолка ПТ8
Св101	12	10,1	24	9,6	96,6	БП7	200	48	с двух концов	люк 300×300 в коробе потолка ПТ8

Сценарии (помещения со светорегуляторами)

Помещение	Сценарий	Горят группы (уровень)	Управление
1. Гостиная-кухня	Вечер	L12 споты гостиной — 30 %; L13 подсветка короба — 100 %; L14 подвесы над столом — 50 %; остальные выкл.	светорегуляторы S9, S10**
	Ужин	L13 подсветка короба — 60 %; L14 подвесы над столом — 100 %; L16 подсветка столешницы — 30 %; остальные выкл.	светорегуляторы S9, S10**, S11**
	Кино	L13 подсветка короба — 20 %; остальные выкл.	светорегулятор S9
	Готовка	L12 споты гостиной — 50 %; L15 споты кухни — 100 %; L16 подсветка столешницы — 100 %; остальные выкл.	светорегуляторы S9, S10**, S11**

Допущения и предложения на листе

Основа листа: взаимное расположение помещений, контур дома 9600 × 8000 и раскладка этажей подобраны проектировщиком под габариты помещений брифа; обмер и проект АР — задание (К-1); высота потолка 2900 мм — по брифу, не замерена; перекрытие 330 мм и отметка 2-го этажа +3,230 приняты; проект КР — задание (К-2); наружные стены 400 мм, перегородки 120 мм приняты (в брифе толщин нет) (К-1); разрешённая мощность 15 кВт принята по типовым ТУ для частного дома (К-4); подрайон климата не задан — принят не северный (жилые от 2,5 м) (К-7).

Знак «**» — предложение проектировщика, заказчиком не утверждено (согласовать с заказчиком): S10, S11 — светорегулятор добавлен разработчиком проекта; Св42, Св43, Св44, Св49, БП5 — диммируемость добавлена разработчиком проекта под светорегуляторы S10 и S11; Св52 — Сдвиг под раскладку плитки стены А на 49 мм вдоль стены — ось на шве или в центре плитки, привязка по таблице листа; Св30 — открытая лента в накладном профиле вместо «в коробе»: короба в потолке нет — подвесной потолок помещения без короба и ниши LED; ИЗ-1: Св15 — Бра над умывальником См4 — по оси раковины (offset 1100).

См. лист открытых вопросов (лист 7, записи К-1, К-2, К-4; лист 8, запись К-7; лист 9, запись ИЗ-1).

Примечания

1. Позиции и марки Св — те же, что на плане освещения (листы 36, 37) и в ведомости светильников (лист 40); группы L — по плану выключателей (листы 38, 39).
2. Модели светильников не выбраны: лист — техническое задание на подбор. Модель по строке таблицы: поток, Тц, Ra, угол, IP и регулировка яркости не хуже указанных, мощность не больше; встраиваемые — под глубину короба (графа «Установка»). IP 20 — сухие помещения. После выбора моделей (артикул, производитель) лист выпускается как «Спецификация светильников».
3. Длина LED-ленты в карнизе и нише уровня — по линиям карниза и ниши плана потолков (листы 66, 67); Σ P = Вт/м × длина. Блок питания загружен не больше чем на 80 %; лента 24 В длиннее 10 м питается с двух концов; доступ к блоку питания — люк ревизии 300×300 мм или место, указанное в таблице.
4. Сценарии: % — яркость группы на светорегуляторе; «вкл.» — группа на обычной клавише; группы, не названные в строке, выключены. Светильники и блоки питания групп на светорегуляторе — с регулировкой яркости. Клавиши и светорегуляторы — листы 38, 39.
5. В пом. 3, 6, 7, 12 свет включается клавишами групп — листы 38, 39.
6. Мощность и поток в таблице — требования к подбору (поток не меньше, мощность не больше указанных); после выбора модели — по её паспорту, Σ P — установленная мощность освещения. Оценка освещённости — на плане освещения; это не светотехнический расчёт.
7. Окончание: «Слои света по помещениям» — лист 65.

Изм.	Кол.уч	Лист	№ док.	Подп.	Дата
Разраб.		Кырлан А.С.			04.11.26
Пров.					
ГИП					
Н. контр.					
Утв.					

ГД-2026-012-АИ

Дом 120 м²

Общая площадь 147,36* м² · * размеры приняты, не замерены (реестр — л. 7–9, К-1)

Дизайн-проект интерьера

Стадия	Лист	Листов
РП	64	175

Техническое задание на подбор светильников

М б/м

Кырлан Александр Сергеевич

выпуск 04.11.2026 № 4dfa962484 · стр. 66 из 180

Техническое задание на подбор светильников (продолжение)

Продолжение таблиц · б/м

Слои света по помещениям

Пом.	Помещение	Слои света — группы включения (марки — в спецификации)	Σ P, Вт
1	Гостиная-кухня	общий — L12, L14, L15; рабочий — L16; акцентный — L13	401,4
2	Холл с лестницей	общий — L10, L80	26
3	Кабинет	общий — L7; акцентный — L8	138,7
4	Санузел гостевой	общий — L17; рабочий — L18	21
5	Прихожая	общий — L10; ночной — L11	50,6
6	Спальня родителей	общий — L1; рабочий — L3; акцентный — L2	151,1
7	Детская	общий — L7; рабочий — L9; акцентный — L8	186,8
8	Гардеробная	общий — L6	10
9	Кладовая	общий — L3	9
10	Холл второго этажа	общий — L10	14
11	Коридор второго этажа	общий — L84	14
12	Детская вторая	общий — L7; рабочий — L9; акцентный — L8	168,6
13	Санузел второго этажа	общий — L4; рабочий — L5	26

Слои света

общий — равномерный свет помещения, по норме освещённости

рабочий — местный свет задачи: столешница, зеркало, чтение у кровати

акцентный — подсветка потолка, стен и ниш; не входит в поток общего света

ночной — путь спальня → санузел: не выше 2700 K, малая яркость, датчик движения

Примечания

1. Продолжение листа 64: позиции, марки и группы — те же, что на основном листе.
2. Σ P — установленная мощность освещения помещения, Вт; группы L — по плану выключателей.

Допущения и предложения на листе

Основа листа: взаимное расположение помещений, контур дома 9600 × 8000 и раскладка этажей подобраны проектировщиком под габариты помещений брифа; обмер и проект АР — задание (К-1); высота потолка 2900 мм — по брифу, не замерена; перекрытие 330 мм и отметка 2-го этажа +3,230 приняты; проект КР — задание (К-2); наружные стены 400 мм, перегородки 120 мм приняты (в брифе толщин нет) (К-1); разрешённая мощность 15 кВт принята по типовым ТУ для частного дома (К-4); подрайон климата не задан — принят не северный (жилые от 2,5 м) (К-7).

См. лист открытых вопросов (лист 7, записи К-1, К-2, К-4; лист 8, запись К-7).

Изм.	Кол.уч	Лист	№ док.	Подп.	Дата
Разраб.		Кырлан А.С.			04.11.26
Пров.					
ГИП					
Н. контр.					
Утв.					

ГД-2026-012-АИ

Дом 120 м²

Общая площадь 147,36* м² · * размеры приняты, не замерены (реестр — л. 7–9, К-1)

Дизайн-проект интерьера

Стадия	Лист	Листов
РП	65	175


Техническое задание на подбор светильников (продолжение)

М б/м

Кырлан Александр Сергеевич

План потолков · 1-й этаж

Уровни и марки потолков, короба с подсветкой, ниши под шторы, люки, вырезы · отметки низа от ±0,000 (чистый пол 1-го этажа) · размеры в мм

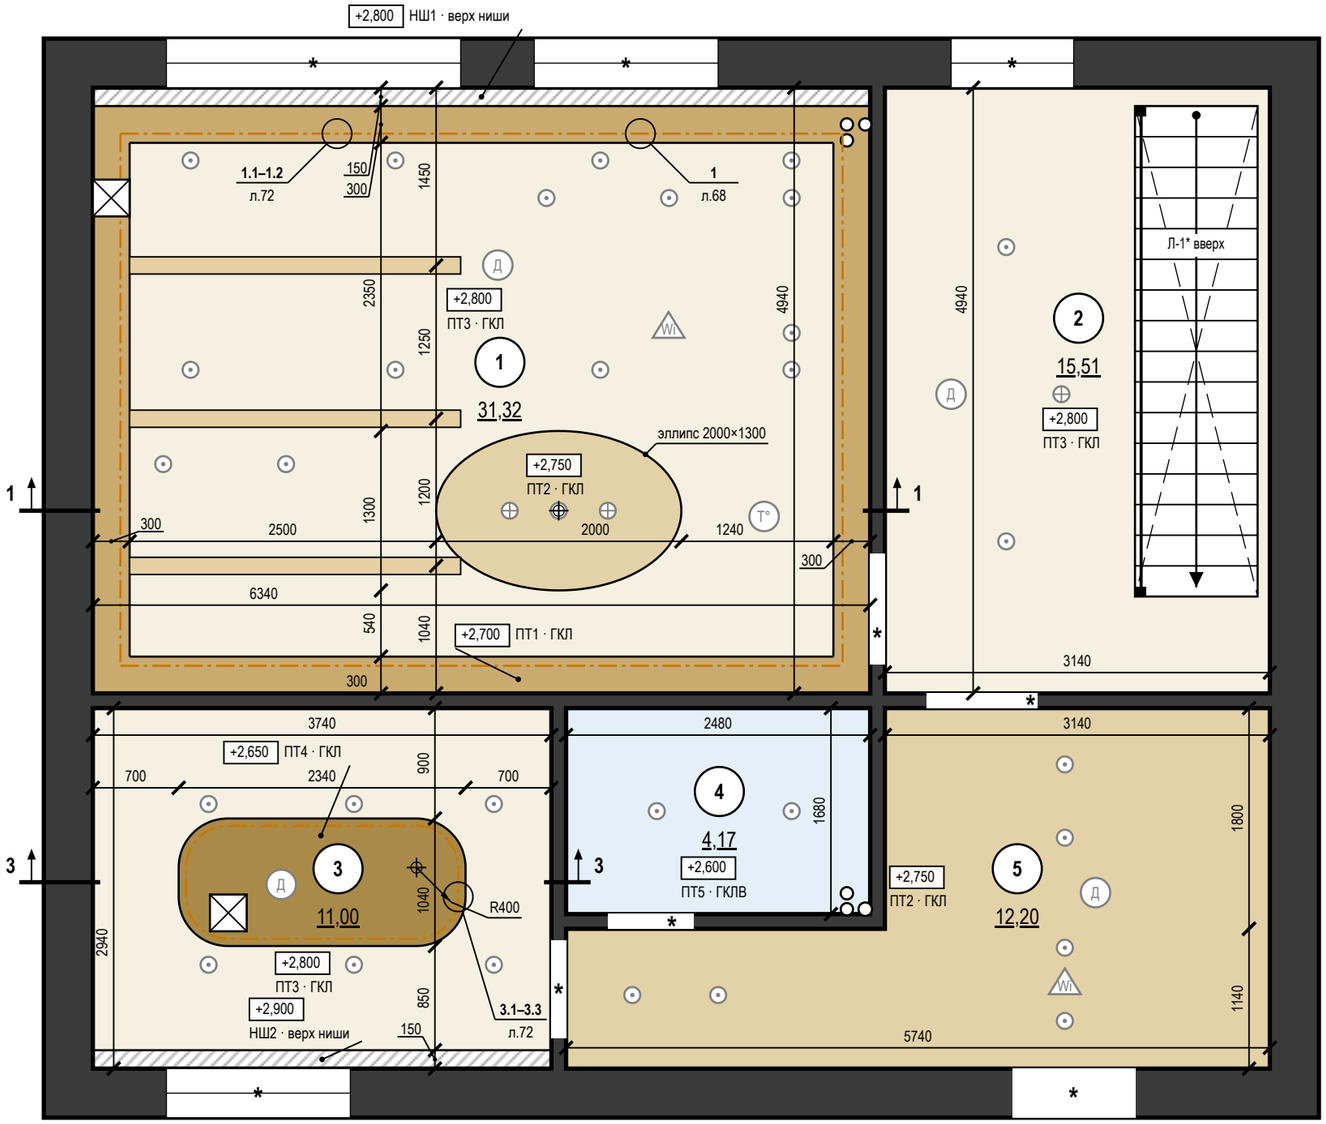

Ведомость потолков

Пом.	Марка	Конструкция	Низ / верх ниши	S, м²	Q
1	ПТ1	ГКЛ П113, короб LED	+2,700	6,32	Q3
1	ПТ2	ГКЛ П113, эллипс	+2,750	2,04	Q3
1	ПТ3	ГКЛ П113	+2,800	22,01	Q3
1	НШ1	ниша под шторы 150×100	+2,800	0,95	
2	ПТ3	ГКЛ П113	+2,800	11,51	Q3
3	ПТ4	ГКЛ П113, остров + LED	+2,650	2,30	Q3
3	ПТ3	ГКЛ П113	+2,800	8,14	Q3
3	НШ2	ниша под шторы 150×100	+2,900	0,56	
4	ПТ5	ГКЛВ П113	+2,600	4,17	Q3
5	ПТ2	ГКЛ П113	+2,750	12,20	Q3
		Итого		**70,20**	

Условные обозначения

- ПТ1 — ГКЛ по каркасу П113, низ +2,700, пояс-короб с карнизом LED
- ПТ2 — ГКЛ по каркасу П113, низ +2,750
- ПТ3 — ГКЛ по каркасу П113, низ +2,800
- ПТ4 — ГКЛ по каркасу П113, низ +2,650
- ПТ5 — ГКЛВ по каркасу П113, низ +2,600
- НШ1 — ниша под шторы 150×100, верх +2,800
- НШ2 — ниша под шторы 150×100, верх +2,900
- граница уровней потолка (перепад)
- проём лестницы в перекрытии: потолка нет, по кромке — борт ГКЛ до перекрытия
- LED-лента в нише подсветки (карниз короба, ниша фигуры)
- стояк: К1 — канализация, В1 — ХВС, Т3 — ГВС
- балка декоративная 140×100 мм
- люк ревизии в потолке 300×300 мм (доступ к БП LED)
- светильник встраиваемый — подложка с плана освещения
- светильник подвесной — подложка с плана освещения
- Д — извещатель дымовой на потолке — подложка
- T° — извещатель тепловой на потолке — подложка
- Wi — точка доступа Wi-Fi на потолке — подложка
- линия разреза у стен помещения, стрелка — направление взгляда
- место узла и сечений М 1:10: номер узла или сечений на полке, под полкой лист
- +2,600 — отметка низа потолка, м (у ниши под шторы — верх ниши); под ней марка потолка
- 1 — номер помещения, площадь м²

Примечания

1. За отметку ±0,000 принят уровень чистого пола сухих помещений 1-го этажа (готовое покрытие), а не существующего пола; пол пом. 4 — −0,015; верх плиты перекрытия −0,064 — расчётный по пирогу пола, не замерен; существующий пол снимается до плиты, его отметка не замерена. Отметки в прямоугольниках — низ потолка; низ перекрытия +2,900. Марка потолка — одна конструкция и отметка на весь альбом.
2. Потолки ГКЛ — каркасная система П113: подвесы через 1000 (с запасом: СП 163, табл. 14 — до 1100 при 0,15 кН/м²), несущие профили через 500, основные через 1200 мм; листы — поперёк несущих профилей. В помещениях 4 — ГКЛВ на оцинкованном каркасе.
3. Нижний уровень — пояс-короб по периметру шириной 300 мм (карниз подсветки + 150 мм полки), верхний — поле внутри пояса: пом. 1.
4. LED-лента в алюминиевом профиле посередине карниза короба шириной 300 мм (узел 1, лист 68); длина по плану: пом. 1 — 20,5 м (в плане освещения 20,5).
5. Балки декоративные 140×100 мм, фальш-балка, массив сосны, белёная (известковая морилка): пом. 1 — 3 шт., 8,1 м, низ +2,700; крепление — на закладной брус 50×50 к каркасу П113, саморезы скрыто.
6. Ниши под шторы 150×100 мм — на всю длину стены с окном; карниз — на закладной до обшивки (узел 2 — пом. 1, лист 68; узел 4 — пом. 3, лист 70).
7. Светильники и потолочные устройства — подложка с планов освещения, слаботочных систем и вентиляции (положение — по ним); вырезы и закладные — по ведомости на листе, до обшивки; отверстия не совмещать с профилями, глубина корпуса светильника до 70 мм.
8. Разрезы 1–1 — лист 68; 3–3 — лист 69; высоты мебели и дверных блоков сверены с низом потолка в разрезах; гибка бортов фигур и ленты ниш — там же; размеры фигурных уровней — фрагменты 1 (лист 69); 2 (лист 70).
9. Узлы по выноскам на плане: узлы 1, 2 — лист 68; узел 3 — лист 69; узел 4 — лист 70; сечения М 1:10 по помещениям — лист 72.
10. Шпаклевание ГКЛ и условия приёмки — Q3: рассеянный дневной свет, осмотр с 2 м; боковой свет не оценивается.
11. Ведомость вырезов и закладных в потолке (1-й этаж) — на листе 71; вырезы и закладные — до обшивки.
12. Люки ревизии 300×300 мм — по центру блоков питания LED (БП4, БП2; координаты — план освещения).
13. Пом. 2: над маршем лестницы Л-1* — проём перекрытия 1000×4000 мм; потолок ГКЛ по кромке проёма закрыт бортом до перекрытия (ГКЛ по ПН 28×27, длина кромки 10,0 м); светильники и устройства в проёме не ставятся.

1000 мм · печать 1:1

Допущения и предложения на листе. Знак «*» принято (замерить): Ст К1-1, Ст В1-1, Ст Т3-1, Ст К1-2 (кухня), Ст В1-2, Ст Т3-2. См. лист открытых вопросов (листы 7–9).

Условные обозначения (продолжение)

Изм.	Кол.уч	Лист	№ док.	Подп.	Дата
Разраб.		Кырлан А.С.			04.11.26
Пров.					
ГИП					
Н. контр.					
Утв.					

ГД-2026-012-АИ

Дом 120 м²

Общая площадь 147,36* м² · * размеры приняты, не замерены (реестр — л. 7–9, К-1)

Дизайн-проект интерьера

Стадия	Лист	Листов
РП	66	175

План потолков · 1-й этаж

М 1:50

Кырлан Александр Сергеевич

ПРЕДВАРИТЕЛЬНО · не для производства работ · открыто пунктов: 11 (реестр — л. 7–9)

выпуск 04.11.2026 № 4dfa962484 · стр. 68 из 180


План потолков · 2-й этаж

Уровни и марки потолков, короба с подсветкой, ниши под шторы, люки, вырезы · отметки низа от ±0,000 (чистый пол 1-го этажа) · размеры в мм

ПРЕДВАРИТЕЛЬНО · не для производства работ · открыто пунктов: 11 (реестр — л. 7–9)

Условные обозначения (продолжение)

Допущения и предложения на листе. Основа листа: взаимное расположение помещений, контур дома 9600 × 8000 и раскладка этажей подобраны проектировщиком под габариты помещений брифа; обмер и проект АР — задание (К-1); высота потолка 2900 мм — по брифу, не замерена; перекрытие 330 мм и отметка 2-го этажа +3,230 приняты; проект КР — задание (К-2); наружные стены 400 мм, перегородки 120 мм приняты (в брифе толщин нет) (К-1); разрешённая мощность 15 кВт принята по типовым ТУ для частного дома (К-4); подрайон климата не задан — принят не северный (жилые от 2,5 м) (К-7). Знак «*» — принято, не замерено (замерить): К-2: отметка чистого пола этажа «2-й этаж» +3,230; К-3: Л-1; К-5: Ст К1-1, Ст В1-1, Ст Т3-1, Ст К1-2 (кухня), Ст В1-2, Ст Т3-2. См. лист открытых вопросов (лист 7, записи К-1–К-5; лист 8, запись К-7).

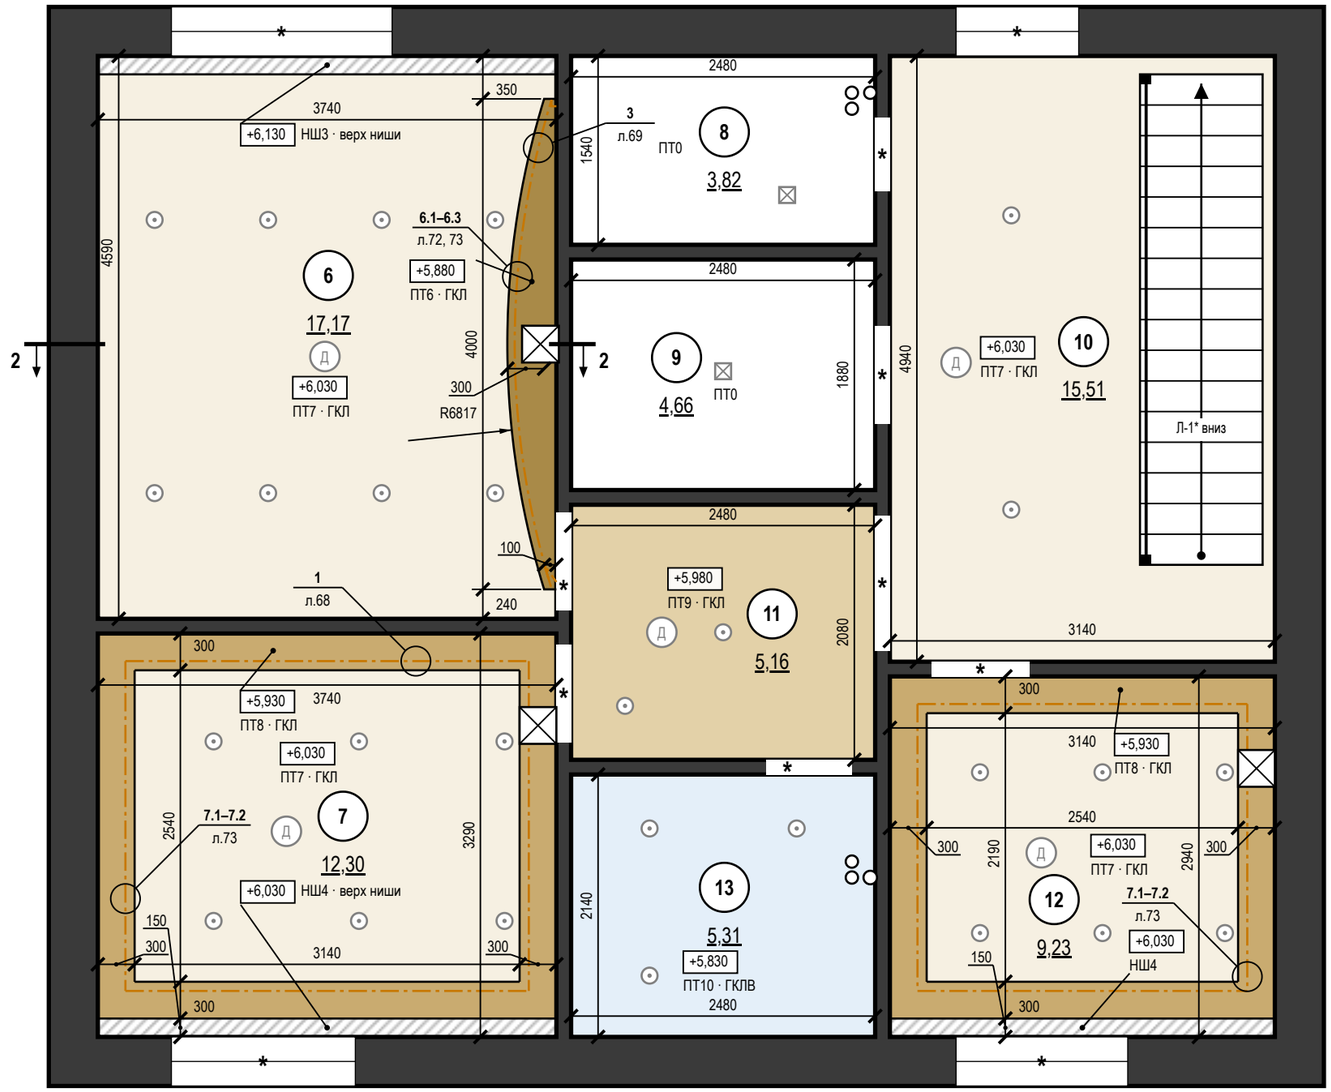

Ведомость потолков

Пом.	Марка	Конструкция	Низ / верх ниши	S, м²	Q
6	ПТ6	ГКЛ П113, дуга + LED	+5,880	1,20	Q3
6	ПТ7	ГКЛ П113	+6,030	15,41	Q3
6	НШ3	ниша под шторы 150×100	+6,130	0,56	
7	ПТ8	ГКЛ П113, короб LED	+5,930	3,77	Q3
7	ПТ7	ГКЛ П113	+6,030	7,97	Q3
7	НШ4	ниша под шторы 150×100	+6,030	0,56	
8, 9	ПТ0	Потолок под покраску	+6,130	8,48	
10	ПТ7	ГКЛ П113	+6,030	15,51	Q3
11	ПТ9	ГКЛ П113	+5,980	5,16	Q3
12	ПТ8	ГКЛ П113, короб LED	+5,930	3,20	Q3
12	ПТ7	ГКЛ П113	+6,030	5,56	Q3
12	НШ4	ниша под шторы 150×100	+6,030	0,47	
13	ПТ10	ГКЛВ П113	+5,830	5,31	Q3
		Итого		**73,16**	

Условные обозначения

- ПТ6 — ГКЛ по каркасу П113, низ +5,880
- ПТ7 — ГКЛ по каркасу П113, низ +6,030
- ПТ8 — ГКЛ по каркасу П113, низ +5,930, пояс-короб с карнизом LED
- ПТ9 — ГКЛ по каркасу П113, низ +5,980
- ПТ10 — ГКЛВ по каркасу П113, низ +5,830
- ПТ0 — потолок под покраску, без подвесного потолка, низ +6,130
- НШ3 — ниша под шторы 150×100, верх +6,130
- НШ4 — ниша под шторы 150×100, верх +6,030
- граница уровней потолка (перепад)
- LED-лента в нише подсветки (карниз короба, ниша фигуры)
- стояк: К1 — канализация, В1 — ХВС, Т3 — ГВС
- люк ревизии в потолке 300×300 мм (доступ к БП LED)
- светильник встраиваемый — подложка с плана освещения
- светильник накладной — подложка с плана освещения
- Д — извещатель дымовой на потолке — подложка
- линия разреза у стен помещения, стрелка — направление взгляда
- место узла и сечений М 1:10: номер узла или сечений на полке, под полкой лист
- +2,600 — отметка низа потолка, м (у ниши под шторы — верх ниши); под ней марка потолка
- 1 — номер помещения, площадь м²

Примечания

1. За отметку ±0,000 принят уровень чистого пола 1-го этажа (готовое покрытие), а не существующего пола; чистый пол сухих помещений этажа — +3,230; пол пом. 13 — +3,215; верх плиты перекрытия +3,166 — расчётный по пирогу пола, не замерен; существующий пол снимается до плиты, его отметка не замерена. Отметки в прямоугольниках — низ потолка; низ перекрытия +6,130. Марка потолка одна конструкция и отметка на весь альбом.
2. Потолки ГКЛ — каркасная система П113: подвесы через 1000 (с запасом: СП 163, табл. 14 — до 1100 при 0,15 кН/м²), несущие профили через 500, основные через 1200 мм; листы — поперёк несущих профилей. В помещениях 13 — ГКЛВ на оцинкованном каркасе.
3. Нижний уровень — пояс-короб по периметру шириной 300 мм (карниз подсветки + 150 мм полки), верхний — поле внутри пояса: пом. 7, 12.
4. LED-лента в алюминиевом профиле посередине карниза короба шириной 300 мм (узел 1, лист 68); длина по плану: пом. 7 — 12,0 м (в плане освещения 12); пом. 12 — 10,1 м (в плане освещения 10,1).
5. Ниши под шторы 150×100 мм — на всю длину стены с окном; карниз — на закладной до обшивки (узел 4 — пом. 6, лист 70; узел 2 — пом. 7, 12, лист 68).
6. Светильники и потолочные устройства — подложка с планов освещения, слаботочных систем и вентиляции (положение — по ним); вырезы и закладные — по ведомости на листе, до обшивки; отверстия не совмещать с профилями, глубина корпуса светильника до 70 мм.
7. Разрезы 2–2 — на листе 68; высоты мебели и дверных блоков сверены с низом потолка в разрезах; гибка бортов фигур и ленты ниш — там же; размеры фигурных уровней — фрагмент 3 (лист 70).
8. Узлы по выноскам на плане: узлы 1, 2 — лист 68; узел 3 — лист 69; узел 4 — лист 70; сечения М 1:10 по помещениям — листы 72, 73.
9. Шпаклевание ГКЛ и условия приёмки — Q3: рассеянный дневной свет, осмотр с 2 м; боковой свет не оценивается.
10. Ведомость вырезов и закладных в потолке (2-й этаж) — на листе 68; вырезы и закладные — до обшивки.
11. Люки ревизии 300×300 мм — по центру блоков питания LED (БП1, БП6, БП7; координаты — план освещения).
12. Основание потолка ПТ0 — по проекту КР дома: конструкция перекрытия в исходных данных не задана (открытый вопрос К-2).

1000 мм · печать 1:1

Изм.	Кол.уч	Лист	№ док.	Подп.	Дата
Разраб.		Кырлан А.С.			04.11.26
Пров.					
ГИП					
Н. контр.					
Утв.					

ГД-2026-012-АИ

Дом 120 м²

Общая площадь 147,36* м² · * размеры приняты, не замерены (реестр — л. 7–9, К-1)

Дизайн-проект интерьера

Стадия	Лист	Листов
РП	67	175

План потолков · 2-й этаж

М 1:50

Кырлан Александр Сергеевич


выпуск 04.11.2026 № 4dfa962484 · стр. 69 из 180

Разрезы и узлы потолков

Разрезы по потолкам с отметками уровней · узлы коробов и ниш · ведомость вырезов и закладных · размеры в мм


Разрез 1–1 (М 1:40)

Пом. 1 Гостиная-кухня

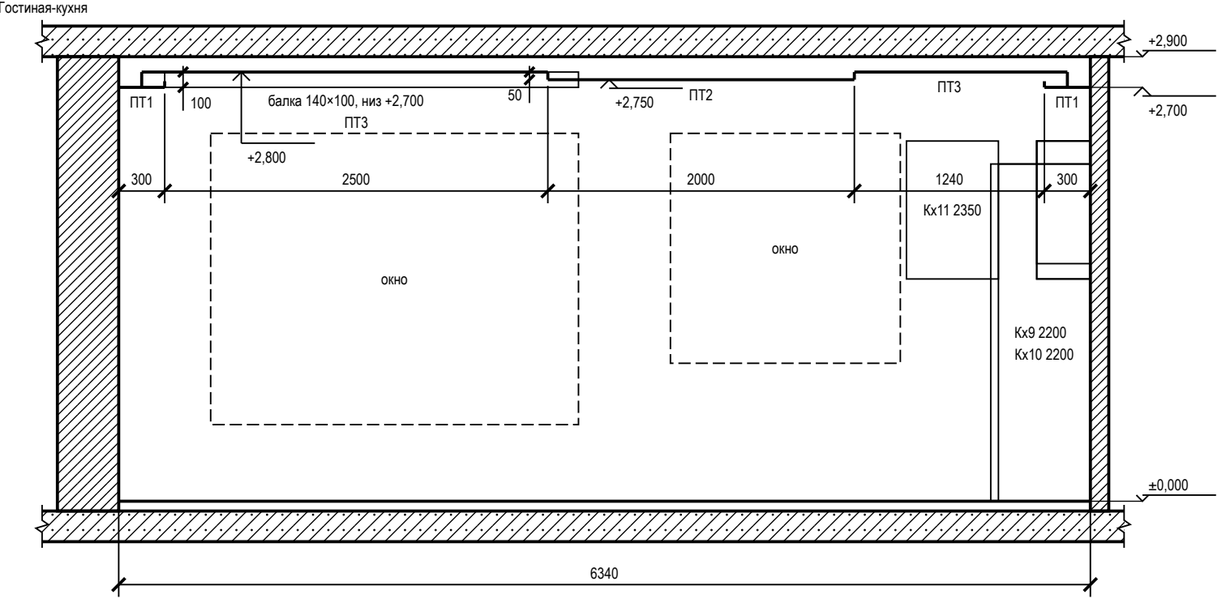


Разрез 2–2 (М 1:40)

Пом. 6 Спальня родителей

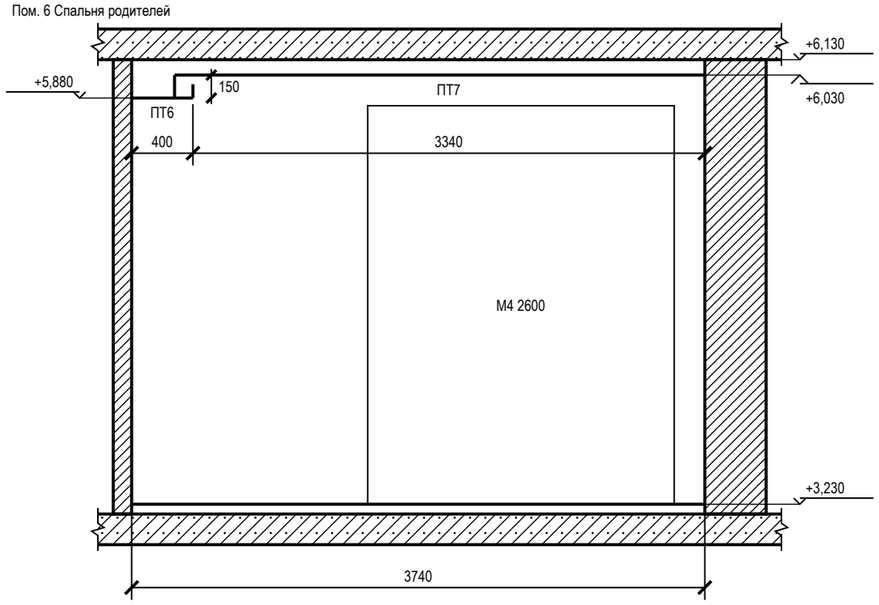

1 Короб с LED-подсветкой (М 1:10)

Пом. 1, 7, 12; карниз 150×100, щель под свет 60 мм

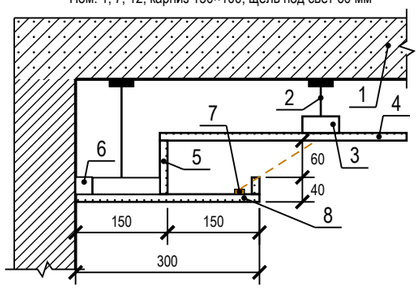


1 — плита перекрытия
2 — подвес прямой, шаг 1000 мм
3 — ПП 60×27: несущие через 500, основные через 1200 мм
4 — ГКЛ 12,5 по П113 — верхний уровень
5 — задняя стенка и бортик карниза — ГКЛ 12,5
6 — ПН 28×27 по периметру, к стене через 500 мм
7 — LED-лента в алюминиевом профиле
8 — низ короба — ГКЛ 12,5 по ПП 60×27

Отметки по помещениям, м

Пом.	низ короба	верх. уровень	низ перекрытия
1	+2,700	+2,800	+2,900
7, 12	+5,930	+6,030	+6,130

2 Ниша под шторы (М 1:10)

Пом. 1, 7, 12; без подсветки; закладные под карниз — до обшивки

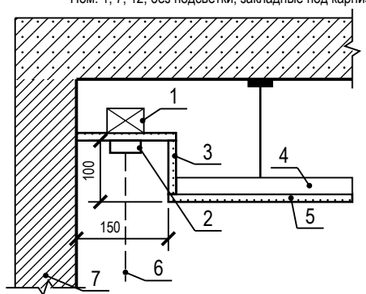

1 — закладная под карниз — брус 40×50
2 — карниз (шина), высота с верхом портьеры 80 мм
3 — стенка и потолок ниши — ГКЛ 12,5
4 — ПП 60×27 — каркас короба
5 — низ короба нижнего уровня — ГКЛ 12,5
6 — портьера
7 — стена с окном

Отметки по помещениям, м

Пом.	низ потолка	верх ниши	низ перекрытия
1	+2,700	+2,800	+2,900
7, 12	+5,930	+6,030	+6,130

Условные обозначения

- плита перекрытия в сечении
- стена в сечении
- потолок ГКЛ в сечении; под линией — марка потолка (план потолков)
- мебель и дверные проёмы за секущей плоскостью; число — марка и верх от чистого пола, мм
- балка декоративная: в сечении — заливка, за плоскостью — тонкой линией; низ балки — подписью у балки или отметкой справа

Ведомость вырезов и закладных в потолке · 2-й этаж

Марка	Устройство	Кол.	Пом.
	Светильник встраиваемый (марки — план освещения)	27	6, 7, 10, 11, 12, 13
	Светильник накладной (марки — план освещения)	2	8, 9
ИП1, ИП8, ИП9**, ИП7**, ИП10	Извещатель дымовой	5	6, 7, 10, 11, 12
	Люк ревизии 300×300	3	6, 7, 12

Допущения и предложения на листе. Основа листа: взаимное расположение помещений, контур дома 9600 × 8000 и раскладка этажей подобраны проектировщиком под габариты помещений брифа; обмер и проект АР — задание (К-1); высота потолка 2900 мм — по брифу, не замерена; перекрытие 330 мм и отметка 2-го этажа +3,230 приняты; проект КР — задание (К-2); наружные стены 400 мм, перегородки 120 мм приняты (в брифе толщин нет) (К-1); разрешённая мощность 15 кВт принята по типовым ТУ для частного дома (К-4); подрайон климата не задан — принят не северный (жилые от 2,5 м) (К-7). Знак «**» — предложение проектировщика, заказчиком не утверждено (согласовать с заказчиком): ИП9, ИП7 — дымовой автономный вместо теплового образца: жилой дом — автономные дымовые в путях эвакуации (СП 486, пункт сверить по действующей редакции). См. лист открытых вопросов (лист 7, записи К-1, К-2, К-4; лист 8, запись К-7).

Примечания

1. Разрезы — по линиям 1–1, 2–2 на плане потолков. Отметки — от ±0,000 (чистый пол 1-го этажа), м; размеры — мм.
2. Высоты мебели и дверных блоков за секущей плоскостью сверены с низом потолка над ними: верх ниже низа короба и поля.
3. ГКЛ 12,5 мм по каркасу П113; перепад уровней и бортик карниза — ГКЛ по ПП 60×27 (узел 1 — на этом листе). Ниша под шторы — на всю длину стены с окном, карниз на закладной до обшивки (узел 2 — на этом листе; узел 4 — лист 70).
4. Толщины плит перекрытия и пирога пола показаны условно.
5. Сечения потолков по помещениям М 1:10 (отметки помещения, профили, подвесы, крепёж, изделия) — листы 72–73.
6. Ведомость вырезов и закладных в потолке (2-й этаж) — к плану потолков: вырезы и закладные — до обшивки, марки светильников — по плану освещения.
7. Ведомость объёмов потолков (лист ГКЛ, профиль, подвесы, лента, блоки питания, люки) — на листе 70.
8. Фрагменты 1, 3, 2 — помещения с фигурными уровнями (размеры фигур, радиусы, отметки) — на листах 69, 70.

1000 мм · печать 1:1

Изм.	Кол.уч	Лист	№ док.	Подп.	Дата
Разраб.		Кырлан А.С.			04.11.26
Пров.					
ГИП					
Н. контр.					
Утв.					

ГД-2026-012-АИ

Дом 120 м²

Общая площадь 147,36* м² · * размеры приняты, не замерены (реестр — л. 7–9, К-1)

Дизайн-проект интерьера

Стадия	Лист	Листов
РП	68	175

Разрезы и узлы потолков

М 1:40; 1:10

Кырлан Александр Сергеевич


выпуск 04.11.2026 № 4dfa962484 · стр. 70 из 180

Разрезы и узлы потолков (продолжение)

Разрезы по потолкам с отметками уровней · узлы коробов и ниш · фрагменты фигурных уровней · размеры в мм


Разрез 3–3 (М 1:40)

Пом. 3 Кабинет

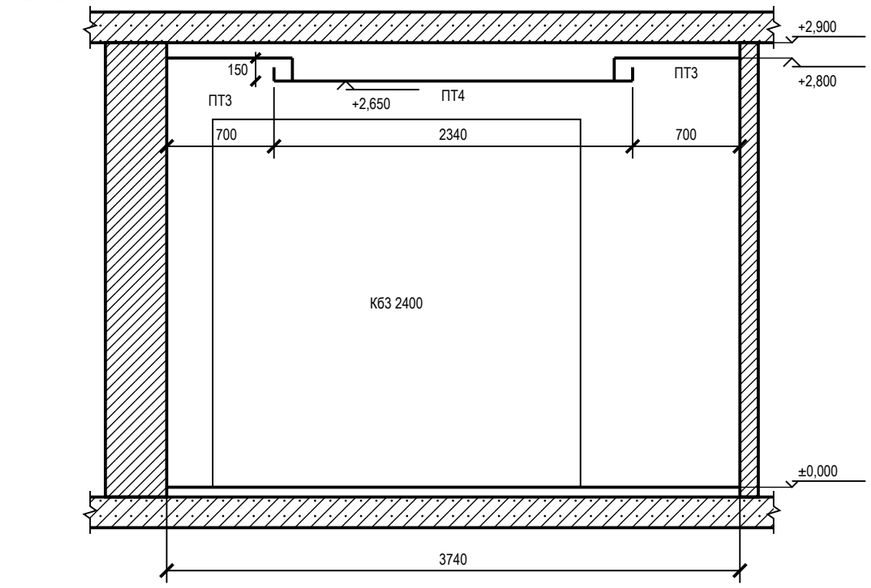


Фрагмент 1. Пом. 1 Гостиная-кухня — уровни потолка (М 1:50)

Цепочки — от чистых граней стен; отметки — низ уровня от ±0,000

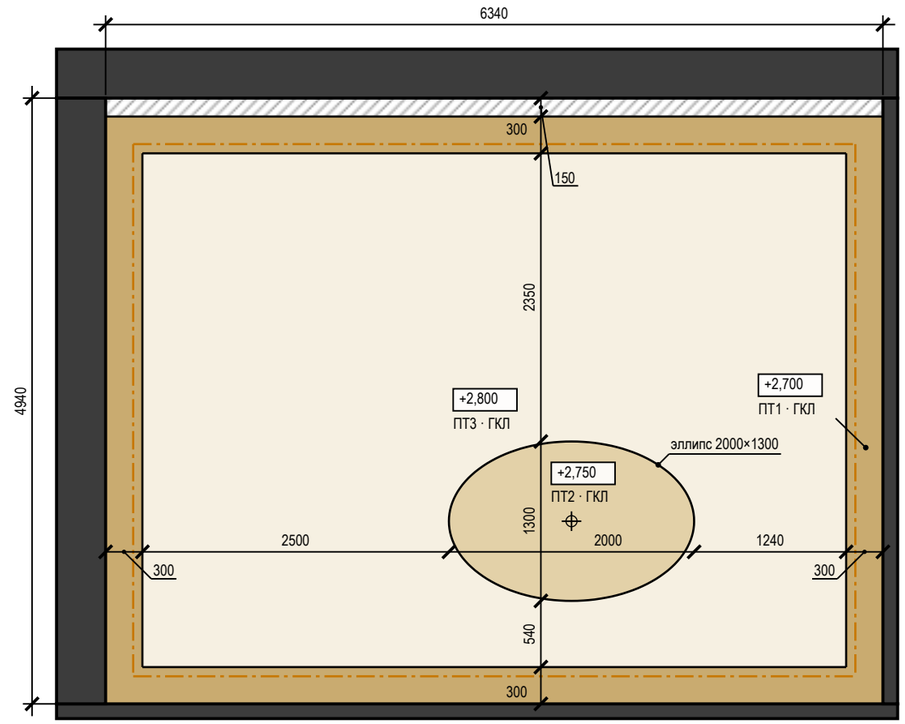

3 Ниша LED фигурного уровня (М 1:10)

Пом. 3, 6; карниз 120×100, щель под свет 60 мм

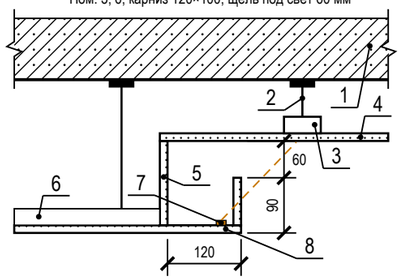

1 — плита перекрытия
2 — подвес прямой, шаг 1000 мм
3 — ПП 60×27: несущие через 500, основные через 1200 мм
4 — ГКЛ 12,5 по П113 — верхний уровень
5 — задняя стенка и бортик карниза — ГКЛ 12,5
6 — ПП 60×27 каркаса нижнего уровня, ПН по контуру фигуры (на дуге — с надрезами)
7 — LED-лента в алюминиевом профиле
8 — низ короба — ГКЛ 12,5 по ПП 60×27

Отметки по помещениям, м

Пом.	низ короба	верх. уровень	низ перекрытия
3	+2,650	+2,800	+2,900
6	+5,880	+6,030	+6,130

Допущения и предложения на листе

Основа листа: взаимное расположение помещений, контур дома 9600 × 8000 и раскладка этажей подобраны проектировщиком под габариты помещений брифа; обмер и проект АР — задание (К-1); высота потолка 2900 мм — по брифу, не замерена; перекрытие 330 мм и отметка 2-го этажа +3,230 приняты; проект КР — задание (К-2); наружные стены 400 мм, перегородки 120 мм приняты (в брифе толщин нет) (К-1); разрешённая мощность 15 кВт принята по типовым ТУ для частного дома (К-4); подрайон климата не задан — принят не северный (жилые от 2,5 м) (К-7).
См. лист открытых вопросов (лист 7, записи К-1, К-2, К-4; лист 8, запись К-7).

Примечания

1. Разрезы — по линиям 3–3 на плане потолков. Отметки — от ±0,000 (чистый пол 1-го этажа), м; размеры — мм.
2. Высоты мебели и дверных блоков за секущей плоскостью сверены с низом потолка над ними: верх ниже низа короба и поля.
3. ГКЛ 12,5 мм по каркасу П113; узлы коробов и ниш под шторы: узел 1 — лист 68; узел 2 — лист 68; узел 4 — лист 70; условные обозначения разрезов — на листе 68.
4. Толщины плит перекрытия и пирога пола показаны условно.
5. Фрагмент 1 — фигурные уровни потолка крупно: привязки краёв и центров фигур к чистым граням стен, радиусы (R) с центрами, хорда и стрелка дуги, отметки низа каждого уровня; цвета уровней — как на плане потолков.
6. Фигурные уровни: борт — ГКЛ по ПН с надрезами (на дуге шаг стоек борта 300 мм при R до 2500, 400 — до 5000) или по гнутому заводскому профилю (СП 163, 6.3.3); гибка: эллипс пом. 1 R423 — ГКЛ 6,5 мокрой гибкой; остров пом. 3 R400 — ГКЛ 6,5 мокрой гибкой; дуга пом. 6 R6817 — ГКЛ 12,5 сухой гибкой (СП 163, табл. 9). Лента в нише фигуры по оси: остров пом. 3 — 5,7 м, дуга пом. 6 — 4,5 м; узел ниши LED фигуры: узел 3 — на этом листе — пом. 3, 6.

1000 мм · печать 1:1

Изм.	Кол.уч	Лист	№ док.	Подп.	Дата
Разраб.		Кырлан А.С.			04.11.26
Пров.					
ГИП					
Н. контр.					
Утв.					

ГД-2026-012-АИ

Дом 120 м²

Общая площадь 147,36* м² · * размеры приняты, не замерены (реестр — л. 7–9, К-1)

Дизайн-проект интерьера

Стадия	Лист	Листов
РП	69	175

Разрезы и узлы потолков (продолжение)

М 1:40; 1:50; 1:10

Кырлан Александр Сергеевич


выпуск 04.11.2026 № 4dfa962484 · стр. 71 из 180

Разрезы и узлы потолков (продолжение)

Узлы коробов и ниш · фрагменты фигурных уровней · ведомость объёмов · размеры в мм

Фрагмент 3. Пом. 6 Спальня родителей — уровни потолка (М 1:50)

Цепочки — от чистых граней стен; отметки — низ уровня от ±0,000

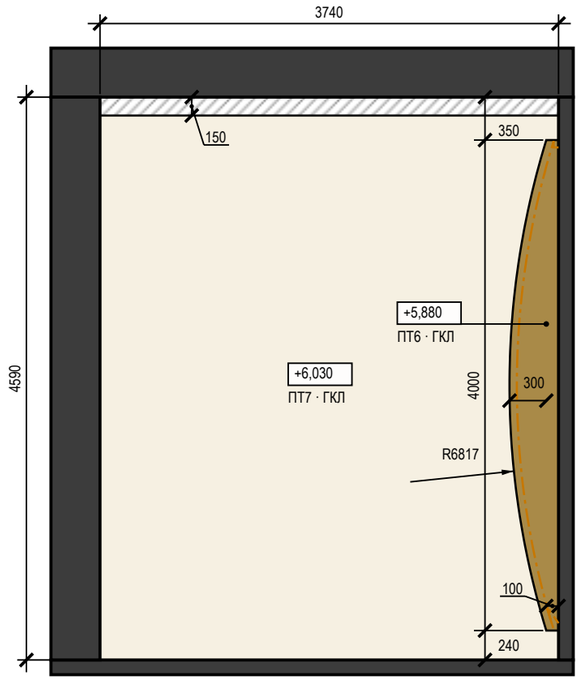


ПТ6 — низ +5,880 · ПТ7 — низ +6,030 · LED-лента в нише подсветки (карниз короба, ниша фигуры) · ниша под шторы

Ведомость объёмов потолков

Позиция	Ед.	Кол.	Пом.
Лист ГКЛ 12,5	м²	143,72	1, 2, 3, 5, 6, 7, 10, 11, 12
Лист ГКЛВ 12,5	м²	9,48	4, 13
Лист ГКЛ арочный 6,5	м²	1,73	1, 3
Борта и карнизы (входят в площади листов выше)	м²	19,19	1, 2, 3, 6, 7, 12
Профиль ПП 60×27	м	405,38	1, 2, 3, 4, 5, 6, 7, 10, 11, 12, 13
Профиль ПН 28×27	м	381,88	1, 2, 3, 4, 5, 6, 7, 10, 11, 12, 13
Подвес прямой	шт.	167	1, 2, 3, 4, 5, 6, 7, 10, 11, 12, 13
Анкер-клин к плите	шт.	167	1, 2, 3, 4, 5, 6, 7, 10, 11, 12, 13
Шуруп TN 3,5×25	шт.	3544	1, 2, 3, 4, 5, 6, 7, 10, 11, 12, 13
Лента армирующая для швов	м	184,88	1, 2, 3, 4, 5, 6, 7, 10, 11, 12, 13
Шпаклёвка для швов	кг	61,63	1, 2, 3, 4, 5, 6, 7, 10, 11, 12, 13
Грунтовка (швы)	л	15,41	1, 2, 3, 4, 5, 6, 7, 10, 11, 12, 13
Лента разделительная по периметру	м	155,16	1, 2, 3, 4, 5, 6, 7, 10, 11, 12, 13
Сплошная шпаклёвка и окраска (площадь развёртки)	м²	154,07	1, 2, 3, 4, 5, 6, 7, 10, 11, 12, 13
Лента LED	м	52,67	1, 3, 6, 7, 12
Требуемая мощность блоков питания	Вт	657	1, 3, 6, 7, 12
Установленная мощность блоков питания	Вт	1100	1, 3, 6, 7, 12
Блок питания LED	шт.	5	1, 3, 6, 7, 12
Люк ревизии	шт.	5	1, 3, 6, 7, 12

Фрагмент 2. Пом. 3 Кабинет — уровни потолка (М 1:50)


Цепочки — от чистых граней стен; отметки — низ уровня от ±0,000

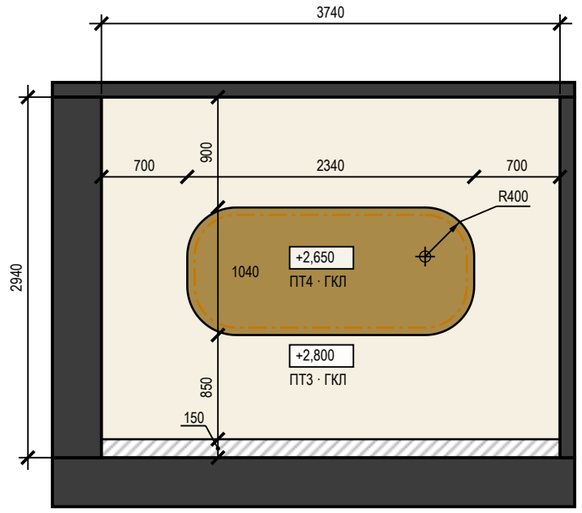

ПТ4 — низ +2,650 · ПТ3 — низ +2,800 · LED-лента в нише подсветки (карниз короба, ниша фигуры) · ниша под шторы

4 Ниша под шторы (М 1:10)

Пом. 3, 6; без подсветки; закладные под карниз — до обшивки

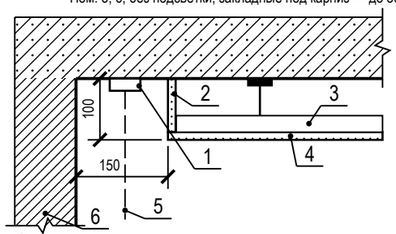

1 — карниз (шина), высота с верхом портьеры 80 мм
2 — стенка ниши — ГКЛ 12,5
3 — ПП 60×27 — каркас короба
4 — низ короба нижнего уровня — ГКЛ 12,5
5 — портьера
6 — стена с окном

Отметки по помещениям, м

Пом.	низ потолка	верх ниши	низ перекрытия
3	+2,800	+2,900	+2,900
6	+6,030	+6,130	+6,130

Допущения и предложения на листе

Основа листа: взаимное расположение помещений, контур дома 9600 × 8000 и раскладка этажей подобраны проектировщиком под габариты помещений брифа; обмер и проект АР — задание (К-1); высота потолка 2900 мм — по брифу, не замерена; перекрытие 330 мм и отметка 2-го этажа +3,230 приняты; проект КР — задание (К-2); наружные стены 400 мм, перегородки 120 мм приняты (в брифе толщин нет) (К-1); разрешённая мощность 15 кВт принята по типовым ТУ для частного дома (К-4); подрайон климата не задан — принят не северный (жилые от 2,5 м) (К-7).
См. лист открытых вопросов (лист 7, записи К-1, К-2, К-4; лист 8, запись К-7).

Примечания

1. ГКЛ 12,5 мм по каркасу П113; узлы коробов и ниш под шторы: узел 1 — лист 68; узел 2 — лист 68; узел 4 — на этом листе; условные обозначения разрезов — на листе 68.
2. Фрагменты 3, 2 — фигурные уровни потолка крупно: привязки краёв и центров фигур к чистым граням стен, радиусы (R) с центрами, хорда и стрелка дуги, отметки низа каждого уровня; цвета уровней как на плане потолков.
3. Ведомость объёмов — по геометрии плана потолков: Лист ГКЛ 12,5 — плоскости уровней + борта (без арочных участков); Лист ГКЛВ 12,5 — плоскости уровней + борта; Лист ГКЛ арочный 6,5 — кривая борта × высота борта и стенки ниши × 2 слоя (R423 мокрая гибка, R400 мокрая гибка); Борта и карнизы — длина перепада × перепад; Профиль ПП 60×27 — S × (1/шаг несущ. + 1/шаг осн.) + стойки бортов; Профиль ПН 28×27 — периметр стен + 2 × перепады + карнизы; Подвес прямой — по раскладке: S уровня / (шаг осн. × шаг подвесов), пояс уже шага — ряд вдоль пояса, фигура — по контуру; шаг подвесов — не больше табл. 14 СП 163; Анкер-клин к плите — по одному на подвес (Knauf П113); Шуруп TN 3,5×25 — 23 шт./м² (Knauf П113, табл. 2 альбома П 11); Лента армирующая для швов 1,2 м/м² листа (Knauf); Шпаклёвка для швов — 0,4 кг/м² листа, только швы (Knauf); Грунтовка (швы) — 0,1 л/м² листа, только швы (Knauf); Лента разделительная по периметру — периметр стен под потолком ГКЛ; Сплошная шпаклёвка и окраска (площадь развёртки) — плоскости + борта; расход — по паспорту материала (норма расхода на сплошной слой не подтверждена); Лента LED — по оси карниза и ниши фигуры (план потолков); Требуемая мощность блоков питания — Вт/м × длина × 1,3; Установленная мощность блоков питания — сумма мощностей блоков по плану освещения; Блок питания LED — блоки потолочных лент по плану освещения (БП4, БП2, БП1, БП6, БП7); Люк ревизии — план потолков; без запаса на подрезку (при закупке листа: ×1,075 при S > 20 м², ×1,175 — 10–20 м², ×1,275 — < 10 м²).

1000 мм · печать 1:1

Изм.	Кол.уч	Лист	№ док.	Подп.	Дата
Разраб.		Кырлан А.С.			04.11.26
Пров.					
ГИП					
Н. контр.					
Утв.					

ГД-2026-012-АИ

Дом 120 м²

Общая площадь 147,36* м² · * размеры приняты, не замерены (реестр — л. 7–9, К-1)

Дизайн-проект интерьера

Стадия	Лист	Листов
РП	70	175

Разрезы и узлы потолков (продолжение)

М 1:50; 1:10

Кырлан Александр Сергеевич

выпуск 04.11.2026 № 4dfa962484 · стр. 72 из 180

Разрезы и узлы потолков (продолжение)

Ведомость вырезов и закладных · размеры в мм

Ведомость вырезов и закладных в потолке · 1-й этаж

Марка	Устройство	Кол.	Пом.
	Светильник встраиваемый (марки — план освещения)	30	1, 2, 3, 4, 5
	Светильник подвесной (марки — план освещения)	4	1, 2
ИП4, ИП6**, ИП2, ИП3**	Извещатель дымовой	4	1, 2, 3, 5
ИП5	Извещатель тепловой	1	1
АР2**, АР1**	Точка доступа Wi-Fi, PoE	2	1, 5
	Люк ревизии 300×300	2	1, 3

Примечания

1. ГКЛ 12,5 мм по каркасу П113; узлы коробов и ниш под шторы: узел 1 — лист 68; узел 2 — лист 68; узел 4 — лист 70; условные обозначения разрезов — на листе 68.
2. Ведомость вырезов и закладных в потолке (1-й этаж) — к плану потолков: вырезы и закладные — до обшивки, марки светильников — по плану освещения.

Допущения и предложения на листе

Основа листа: взаимное расположение помещений, контур дома 9600 × 8000 и раскладка этажей подобраны проектировщиком под габариты помещений брифа; обмер и проект АР — задание (К-1); высота потолка 2900 мм — по брифу, не замерена; перекрытие 330 мм и отметка 2-го этажа +3,230 приняты; проект КР — задание (К-2); наружные стены 400 мм, перегородки 120 мм приняты (в брифе толщин нет) (К-1); разрешённая мощность 15 кВт принята по типовым ТУ для частного дома (К-4); подрайон климата не задан — принят не северный (жилые от 2,5 м) (К-7).

Знак «**» — предложение проектировщика, заказчиком не утверждено (согласовать с заказчиком): ИП6, ИПЗ — дымовой автономный вместо теплового образца: жилой дом — автономные дымовые в путях эвакуации (СП 486, пункт сверить по действующей редакции); АР2, АР1 — точка доступа Wi-Fi: число и места.

См. лист открытых вопросов (лист 7, записи К-1, К-2, К-4; лист 8, запись К-7).

Изм.	Кол.уч	Лист	№ док.	Подп.	Дата
Разраб.		Кырлан А.С.			04.11.26
Пров.					
ГИП					
Н. контр.					
Утв.					

ГД-2026-012-АИ

Дом 120 м²

Общая площадь 147,36* м² · * размеры приняты, не замерены (реестр — л. 7–9, К-1)

Дизайн-проект интерьера

Стадия	Лист	Листов
РП	71	175

Разрезы и узлы потолков (продолжение)

М б/м

Кырлан Александр Сергеевич


выпуск 04.11.2026 № 4dfa962484 · стр. 73 из 180

Сечения потолков М 1:10

Пом. 1, 3, 6 · профили, подвесы, крепёж, изделия · размеры в мм

Сечение 1.1. Короб с LED-подсветкой (М 1:10)


Пом. 1 Гостиная-кухня; карниз 150×100, щель под свет 60 мм

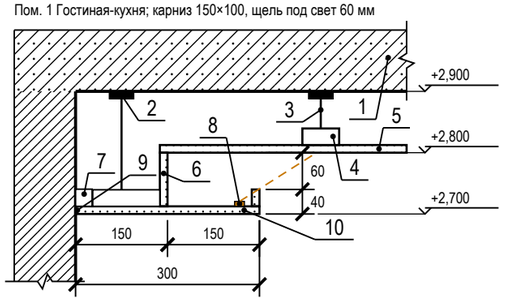

1 — плита перекрытия
2 — анкер-клин к плите — по одному на подвес
3 — подвес прямой, шаг 1000 мм
4 — ПП 60×27: несущие через 500, основные через 1200 мм; соединители одноуровневые, шурупы LN 3,5×9
5 — ГКЛ 12,5 по П113 — верхний уровень; шурупы TN 3,5×25 через 170 мм
6 — задняя стенка и бортик карниза — ГКЛ 12,5
7 — ПН 28×27 по периметру — дюбель-гвоздь через ≤ 500 мм, не менее 3 на профиль
8 — LED-лента 9,6 Вт/м, 24 В в алюминиевом профиле
9 — примыкание к стене — лента разделительная, шов зашпаклёван
10 — низ короба — ГКЛ 12,5 по ПП 60×27

Сечение 1.2. Ниша под шторы (М 1:10)


Пом. 1 Гостиная-кухня; без подсветки; закладные под карниз — до обшивки

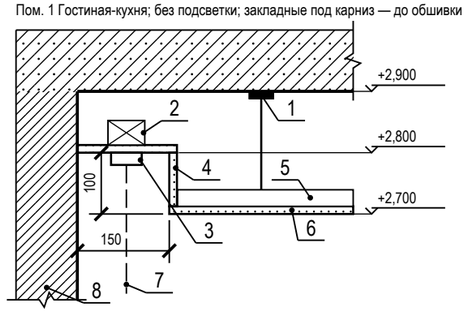

1 — анкер-клин к плите — по одному на подвес; подвес прямой, шаг 1000 мм
2 — закладная под карниз — брус 40×50
3 — карниз (шина), высота с верхом портьеры 80 мм
4 — стенка и потолок ниши — ГКЛ 12,5
5 — ПП 60×27 — каркас короба, основные через 1200 мм; соединители одноуровневые, шурупы LN 3,5×9
6 — низ короба нижнего уровня — ГКЛ 12,5; шурупы TN 3,5×25 через 170 мм
7 — портьера
8 — стена с окном

Сечение 3.1. Ниша LED фигурного уровня (М 1:10)


Пом. 3 Кабинет; карниз 120×100, щель под свет 60 мм

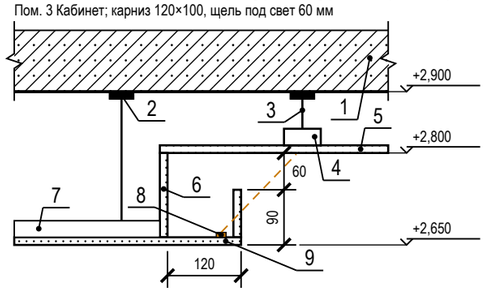

1 — плита перекрытия
2 — анкер-клин к плите — по одному на подвес
3 — подвес прямой, шаг 1000 мм
4 — ПП 60×27: несущие через 500, основные через 1200 мм; соединители одноуровневые, шурупы LN 3,5×9
5 — ГКЛ 12,5 по П113 — верхний уровень; шурупы TN 3,5×25 через 170 мм
6 — задняя стенка и бортик карниза — ГКЛ 12,5
7 — ПП 60×27 каркаса нижнего уровня, ПН по контуру фигуры (на дуге — с надрезами)
8 — LED-лента 9,6 Вт/м, 24 В в алюминиевом профиле
9 — низ короба — ГКЛ 12,5 по ПП 60×27

Сечение 3.2. Ниша под шторы (М 1:10)


Пом. 3 Кабинет; без подсветки; закладные под карниз — до обшивки

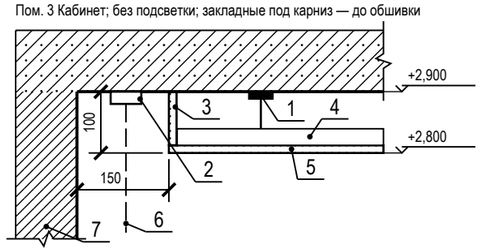

1 — анкер-клин к плите — по одному на подвес; подвес прямой, шаг 1000 мм
2 — карниз (шина), высота с верхом портьеры 80 мм
3 — стенка ниши — ГКЛ 12,5
4 — ПП 60×27 — каркас короба, основные через 1200 мм; соединители одноуровневые, шурупы LN 3,5×9
5 — низ короба нижнего уровня — ГКЛ 12,5; шурупы TN 3,5×25 через 170 мм
6 — портьера
7 — стена с окном

Сечение 3.3. Примыкание потолка к стене (М 1:10)


Пом. 3 Кабинет; примыкание — разделительная лента

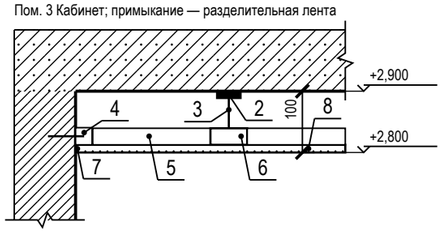

1 — плита перекрытия
2 — анкер-клин к плите — по одному на подвес
3 — подвес прямой, шаг 1000 мм
4 — ПН 28×27 по периметру — дюбель-гвоздь через ≤ 500 мм, не менее 3 на профиль
5 — ПП 60×27 несущий (вид) через 500 мм, в ПН
6 — ПП 60×27 основной (сечение) через 1200 мм; соединители одноуровневые, шурупы LN 3,5×9
7 — лента разделительная по стене, шов зашпаклёван
8 — ГКЛ 12,5 по П113; шурупы TN 3,5×25 через 170 мм

Сечение 6.1. Ниша LED фигурного уровня (М 1:10)

Пом. 6 Спальня родителей; карниз 120×100, щель под свет 60 мм

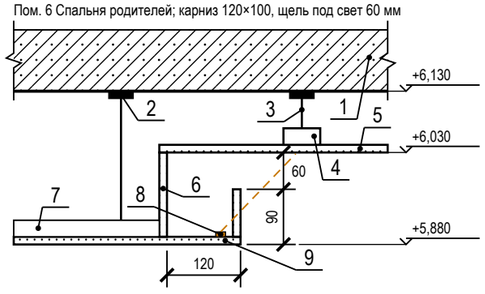

1 — плита перекрытия
2 — анкер-клин к плите — по одному на подвес
3 — подвес прямой, шаг 1000 мм
4 — ПП 60×27: несущие через 500, основные через 1200 мм; соединители одноуровневые, шурупы LN 3,5×9
5 — ГКЛ 12,5 по П113 — верхний уровень; шурупы TN 3,5×25 через 170 мм
6 — задняя стенка и бортик карниза — ГКЛ 12,5
7 — ПП 60×27 каркаса нижнего уровня, ПН по контуру фигуры (на дуге — с надрезами)
8 — LED-лента 9,6 Вт/м, 24 В в алюминиевом профиле
9 — низ короба — ГКЛ 12,5 по ПП 60×27

Условные обозначения

— · — LED-лента в нише подсветки (карниз короба, ниша фигуры)

Допущения и предложения на листе

Основа листа: взаимное расположение помещений, контур дома 9600 × 8000 и раскладка этажей подобраны проектировщиком под габариты помещений брифа; обмер и проект АР — задание (К-1); высота потолка 2900 мм — по брифу, не замерена; перекрытие 330 мм и отметка 2-го этажа +3,230 приняты; проект КР — задание (К-2); наружные стены 400 мм, перегородки 120 мм приняты (в брифе толщин нет) (К-1); разрешённая мощность 15 кВт принята по типовым ТУ для частного дома (К-4); подрайон климата не задан — принят не северный (жилые от 2,5 м) (К-7).
См. лист открытых вопросов (лист 7, записи К-1, К-2, К-4; лист 8, запись К-7).

Примечания

1. Сечения потолков М 1:10 по помещениям с нишами LED и нишами под шторы: отметки и размеры этого помещения от ±0,000 — чистого пола 1-го этажа (м, мм). Положение — по плану потолков (листы 66, 67): короб и ниша LED — по линиям ленты, ниша под шторы — у стены с окном; типовые узлы по группам помещений — на листе 68.
2. Крепёж: подвес прямой к плите на анкер-клине — по одному на подвес (Knauf П113); ПН к стенам — дюбель-гвоздь через ≤ 500 мм, не менее 3 на профиль (серия 1.045.9-2.08); лист 12,5 — шурупы TN 3,5×25 через 170 мм (СП 163, табл. 15); профили между собой — соединители одноуровневые, шурупы LN 3,5×9.
3. Изделие карниза, профиля LED и галтели подписано артикулом из данных; где артикул не выбран, сечение дано по габаритам из данных (ширина и глубина ниши, щель под свет), изделие подбирается по ним.

1000 мм · печать 1:1

Изм.	Кол.уч	Лист	№ док.	Подп.	Дата
Разраб.		Кырлан А.С.			04.11.26
Пров.					
ГИП					
Н. контр.					
Утв.					

ГД-2026-012-АИ

Дом 120 м²

Общая площадь 147,36* м² · * размеры приняты, не замерены (реестр — л. 7–9, К-1)

Дизайн-проект интерьера

Стадия	Лист	Листов
РП	72	175

Сечения потолков М 1:10

М 1:10

Кырлан Александр Сергеевич


выпуск 04.11.2026 № 4dfa962484 · стр. 74 из 180

Сечения потолков М 1:10

Пом. 6, 7, 12 · профили, подвесы, крепёж, изделия · размеры в мм

Сечение 6.2. Ниша под шторы (М 1:10)


Пом. 6 Спальня родителей; без подсветки; закладные под карниз — до обшивки

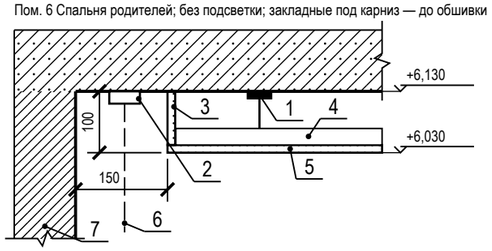

1 — анкер-клин к плите — по одному на подвес; подвес прямой, шаг 1000 мм
2 — карниз (шина), высота с верхом портьеры 80 мм
3 — стенка ниши — ГКЛ 12,5
4 — ПП 60×27 — каркас короба, основные через 1200 мм; соединители одноуровневые, шурупы LN 3,5×9
5 — низ короба нижнего уровня — ГКЛ 12,5; шурупы TN 3,5×25 через 170 мм
6 — портьера
7 — стена с окном

Сечение 6.3. Примыкание потолка к стене (М 1:10)


Пом. 6 Спальня родителей; примыкание — разделительная лента

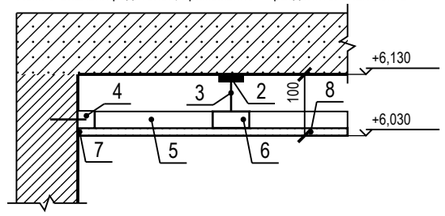

1 — плита перекрытия
2 — анкер-клин к плите — по одному на подвес
3 — подвес прямой, шаг 1000 мм
4 — ПН 28×27 по периметру — дюбель-гвоздь через ≤ 500 мм, не менее 3 на профиль
5 — ПП 60×27 несущий (вид) через 500 мм, в ПН
6 — ПП 60×27 основной (сечение) через 1200 мм; соединители одноуровневые, шурупы LN 3,5×9
7 — лента разделительная по стене, шов зашпаклёван
8 — ГКЛ 12,5 по П113; шурупы TN 3,5×25 через 170 мм

Сечение 7.1. Короб с LED-подсветкой (М 1:10)


Пом. 7 Детская, 12 Детская вторая; карниз 150×100, щель под свет 60 мм

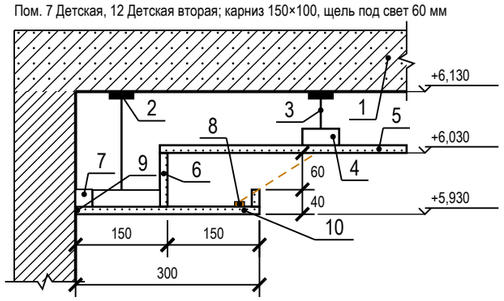

1 — плита перекрытия
2 — анкер-клин к плите — по одному на подвес
3 — подвес прямой, шаг 1000 мм
4 — ПП 60×27: несущие через 500, основные через 1200 мм; соединители одноуровневые, шурупы LN 3,5×9
5 — ГКЛ 12,5 по П113 — верхний уровень; шурупы TN 3,5×25 через 170 мм
6 — задняя стенка и бортик карниза — ГКЛ 12,5
7 — ПН 28×27 по периметру — дюбель-гвоздь через ≤ 500 мм, не менее 3 на профиль
8 — LED-лента 9,6 Вт/м, 24 В в алюминиевом профиле
9 — примыкание к стене — лента разделительная, шов зашпаклёван
10 — низ короба — ГКЛ 12,5 по ПП 60×27

Сечение 7.2. Ниша под шторы (М 1:10)

Пом. 7 Детская, 12 Детская вторая; без подсветки; закладные под карниз — до обшивки

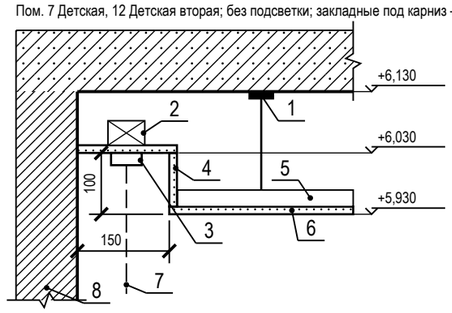

1 — анкер-клин к плите — по одному на подвес; подвес прямой, шаг 1000 мм
2 — закладная под карниз — брус 40×50
3 — карниз (шина), высота с верхом портьеры 80 мм
4 — стенка и потолок ниши — ГКЛ 12,5
5 — ПП 60×27 — каркас короба, основные через 1200 мм; соединители одноуровневые, шурупы LN 3,5×9
6 — низ короба нижнего уровня — ГКЛ 12,5; шурупы TN 3,5×25 через 170 мм
7 — портьера
8 — стена с окном

Условные обозначения

— · — · LED-лента в нише подсветки (карниз короба, ниша фигуры)

Допущения и предложения на листе

Основа листа: взаимное расположение помещений, контур дома 9600 × 8000 и раскладка этажей подобраны проектировщиком под габариты помещений брифа; обмер и проект АР — задание (К-1); высота потолка 2900 мм — по брифу, не замерена; перекрытие 330 мм и отметка 2-го этажа +3,230 приняты; проект КР — задание (К-2); наружные стены 400 мм, перегородки 120 мм приняты (в брифе толщин нет) (К-1); разрешённая мощность 15 кВт принята по типовым ТУ для частного дома (К-4); подрайон климата не задан — принят не северный (жилые от 2,5 м) (К-7).
Знак «*» — принято, не замерено и не подтверждено (замерить на объекте): К-2: отметка чистого пола этажа «2-й этаж» +3,230 — отметка чистого пола 2-го этажа +3,230 принята: высота потолка 2900 по брифу + перекрытие с полом 330 (конструкция перекрытия не задана; проект КР — задание).
См. лист открытых вопросов (лист 7, записи К-1, К-2, К-4; лист 8, запись К-7).

Примечания

1. Сечения потолков М 1:10 по помещениям с нишами LED и нишами под шторы: отметки и размеры этого помещения от ±0,000 — чистого пола 1-го этажа (м, мм). Положение — по плану потолков (листы 66, 67): короб и ниша LED — по линиям ленты, ниша под шторы — у стены с окном; типовые узлы по группам помещений — на листе 68.
2. Крепёж: подвес прямой к плите на анкер-клине — по одному на подвес (Knauf П113); ПН к стенам — дюбель-гвоздь через ≤ 500 мм, не менее 3 на профиль (серия 1.045.9-2.08); лист 12,5 — шурупы TN 3,5×25 через 170 мм (СП 163, табл. 15); профили между собой — соединители одноуровневые, шурупы LN 3,5×9.
3. Изделие карниза, профиля LED и галтели подписано артикулом из данных; где артикул не выбран, сечение дано по габаритам из данных (ширина и глубина ниши, щель под свет), изделие подбирается по ним.

1000 мм · печать 1:1

Изм.	Кол.уч	Лист	№ док.	Подп.	Дата
Разраб.		Кырлан А.С.			04.11.26
Пров.					
ГИП					
Н. контр.					
Утв.					

ГД-2026-012-АИ

Дом 120 м²

Общая площадь 147,36* м² · * размеры приняты, не замерены (реестр — л. 7–9, К-1)

Дизайн-проект интерьера

Стадия	Лист	Листов
РП	73	175

Сечения потолков М 1:10


М 1:10

Кырлан Александр Сергеевич


Раскладка плитки. Планы полов

Раскладка от чистовых размеров · размеры в мм · отметки от ±0,000 (чистый пол 1-го этажа)

Фрагмент 1. Санузел гостевой (пом. 4). Пол 600×600, шов 2 мм, М 1:25

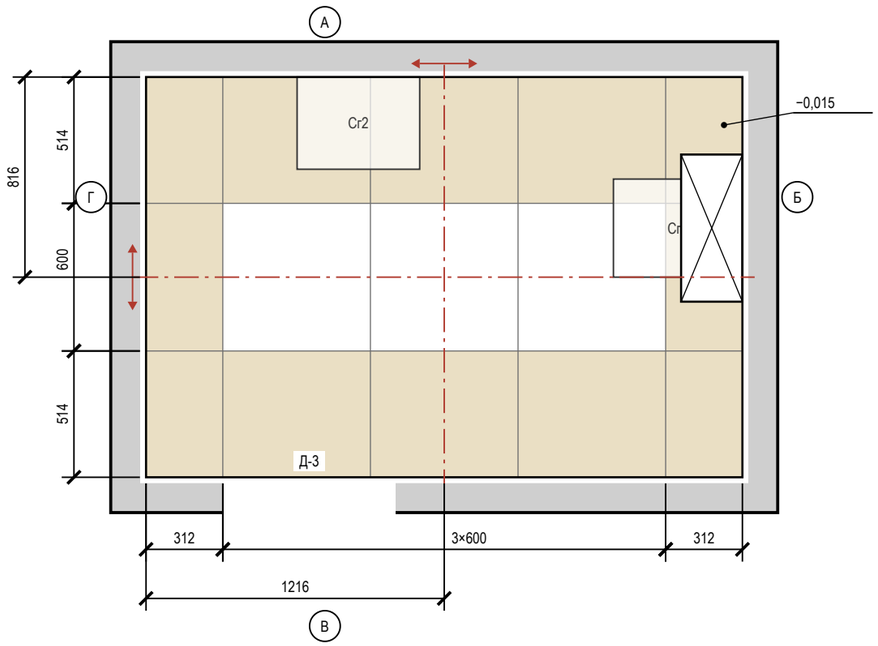

Фрагмент 2. Санузел второго этажа (пом. 13). Пол 600×600, шов 2 мм, М 1:25

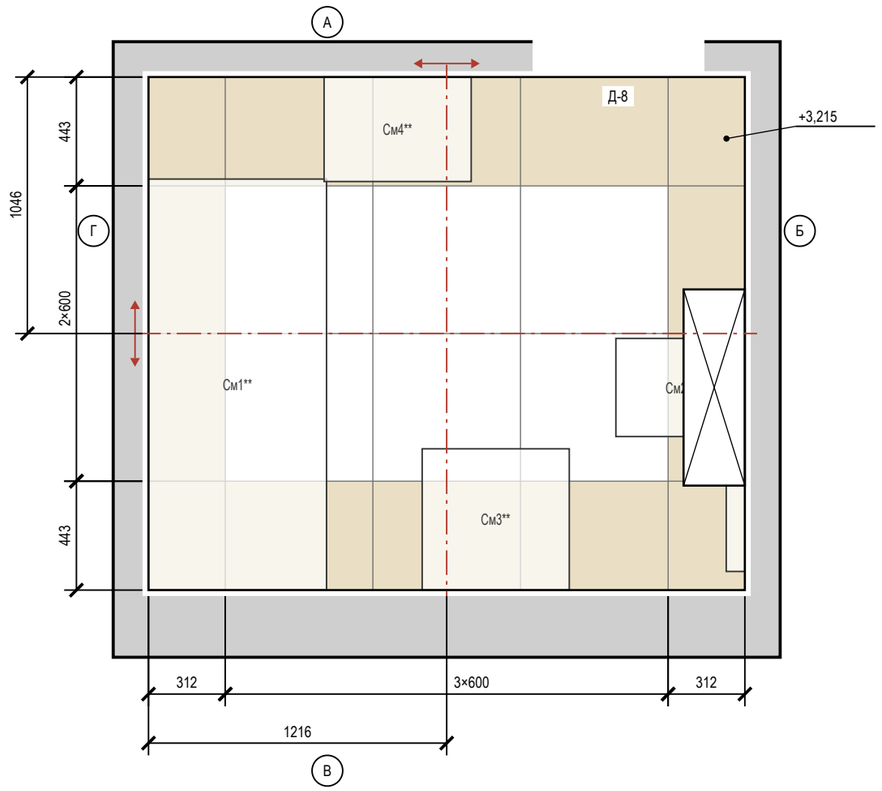

Примечания

1. Раскладка от чистовых размеров: стены санузлов теряют 10 + 5 + 9 = 24 мм на сторону (штукатурка, клей, плитка); подрезки чистые, без шва.
2. Старт — от центра помещения (штрихпунктир, стрелки направление укладки); размер старта — от чистовых стен Г и А.
3. Раскладка пола «Прихожая» и фартука «Гостиная-кухня» и фартука «Гостиная-кухня» — на листе «Раскладка плитки. Прихожая. Фартук кухни».
4. Калибр партии не задан — до укладки замерить (рабочий размер W, ГОСТ 13996-2019) и пересчитать подрезки.
5. Количество: целые по раскладке + по одной на подрезку, запас 10 %; один артикул — одна партия и тон. Исключены поддон, короб, проёмы и места за коробом; S — по чистым граням: стены нетто = зона облицовки по ведомости отделки − место за коробом инсталляции 1,68 м² (плитку за коробом не кладут), короб отдельной строкой.
6. Клей C2 TE S1 Ceresit CM 17; C2 TE S1 (ГОСТ Р 56387-2018), затирка CG2WA Mapei Ultracolor Plus 132; CG2WA; расход — по ТУ выбранной марки.
7. Гидроизоляция: пол и стены 200 мм от ЧП; над ванной — до 2000 и 300 мм за борт (пом. 13) (см. развёртки); акт скрытых работ, пролив 24 ч.
8. Швы пола совмещены со швами стены А; по периметру — демпферная лента.
9. Отметка чистого пола −0,015, +3,215, порог 15 мм; стык с соседним покрытием — по оси полотна двери.

Условные обозначения

- плитка целая; тонкая линия — шов
- плитка с подрезкой (размер — на цепочке)
- ось старта; стрелки — направление укладки
- сантехприбор: габарит, высота по практике
- короб инсталляции: плитка пола — до короба
- отметка чистого пола на полке выноски, м
- (А) обозначение стены А–Г (как на развёртках)

Допущения и предложения на листе. Основа листа: взаимное расположение помещений, контур дома 9600 × 8000 и раскладка этажей подобраны проектировщиком под габариты помещений брифа; обмер и проект АР — задание (К-1); высота потолка 2900 мм — по брифу, не замерена; перекрытие 330 мм и отметка 2-го этажа +3,230 приняты; проект КР — задание (К-2); наружные стены 400 мм, перегородки 120 мм приняты (в брифе толщин нет) (К-1); разрешённая мощность 15 кВт принята по типовым ТУ для частного дома (К-4); подрайон климата не задан — принят не северный (жилые от 2,5 м) (К-7). Знак «**» — предложено, не утверждено (согласовать): пол пом. 4, 13; ИЗ-1: См1, См2, См3; К-9: См4. См. лист открытых вопросов (лист 7, записи К-1, К-2, К-4; лист 8, записи К-7, К-9; лист 9, запись ИЗ-1).

Ведомость плитки

Помещение, поверхность	Плитка, код	Формат	Шов	S, м²	Целых	Подр.	С запасом
Санузел гостевой, пол	аналог: керамогранит под травертин	600×600	2	4,17	3	12	17
Санузел гостевой, стены А–Г	A8UZ	600×1200	2	16,68	11	21	36
Санузел гостевой, короб инсталляции	A8UZ	600×1200	2	1,47	1	3	5
Санузел второго этажа, пол	аналог: керамогранит под травертин	600×600	2	5,31	6	14	22
Санузел второго этажа, стены А–Г	A8UZ	600×1200	2	18,10	16	19	39
Санузел второго этажа, короб инсталляции	A8UZ	600×1200	2	1,76	0	6	7
Прихожая, пол	A8UZ	600×1200	2	12,20	4	22	29
Гостиная-кухня, фартук (ст. А)	аналог: керамогранит под травертин, матовый	1200×600	2	0,89	0	3	4
Гостиная-кухня, фартук (ст. Б)	аналог: керамогранит под травертин, матовый	1200×600	2	1,05	0	4	5
Итого 600×600				9,48	9	26	39
Итого 600×1200				**52,15**	**32**	**78**	**125**

Ведомость материалов

Материал	Класс, код	Норма расхода	Кол-во
Затирка	CG2WA Mapei Ultracolor Plus 132	(a+b)/ab·шов·t·1,6	4,1 кг
Затирка	CG2WA	(a+b)/ab·шов·t·1,6	1,1 кг
Клей	C2 TE S1 Ceresit CM 17	1,5 кг/м²·мм, слой 5	402 кг (17 меш.)
Клей	C2 TE S1	1,5 кг/м²·мм, слой 5	115 кг (5 меш.)
Гидроизоляция	обмазочная, 2 слоя: пол, стены по периметру и зоны замачивания	по ТУ	19,6 м²
Демпф. лента	по периметру пола из плитки		33,3 м

1000 мм · печать 1:1

Изм.	Кол.уч	Лист	№ док.	Подп.	Дата
Разраб.		Кырлан А.С.			04.11.26
Пров.					
ГИП					
Н. контр.					
Утв.					

ГД-2026-012-АИ

Дом 120 м²

Общая площадь 147,36* м² · * размеры приняты, не замерены (реестр — л. 7–9, К-1)

Дизайн-проект интерьера

Стадия	Лист	Листов
РП	74	175

Раскладка плитки. Планы полов

М 1:25

Кырлан Александр Сергеевич


выпуск 04.11.2026 № 4dfa962484 · стр. 76 из 180

Раскладка плитки. Прихожая. Фартук кухни


Раскладка от чистовых размеров · размеры в мм · высоты фартука от чистого пола

ПРЕДВАРИТЕЛЬНО · не для производства работ · открыто пунктов: 11 (реестр — л. 7–9)


Фрагмент 1. Прихожая (пом. 5). Пол 600×1200, шов 2 мм, М 1:40

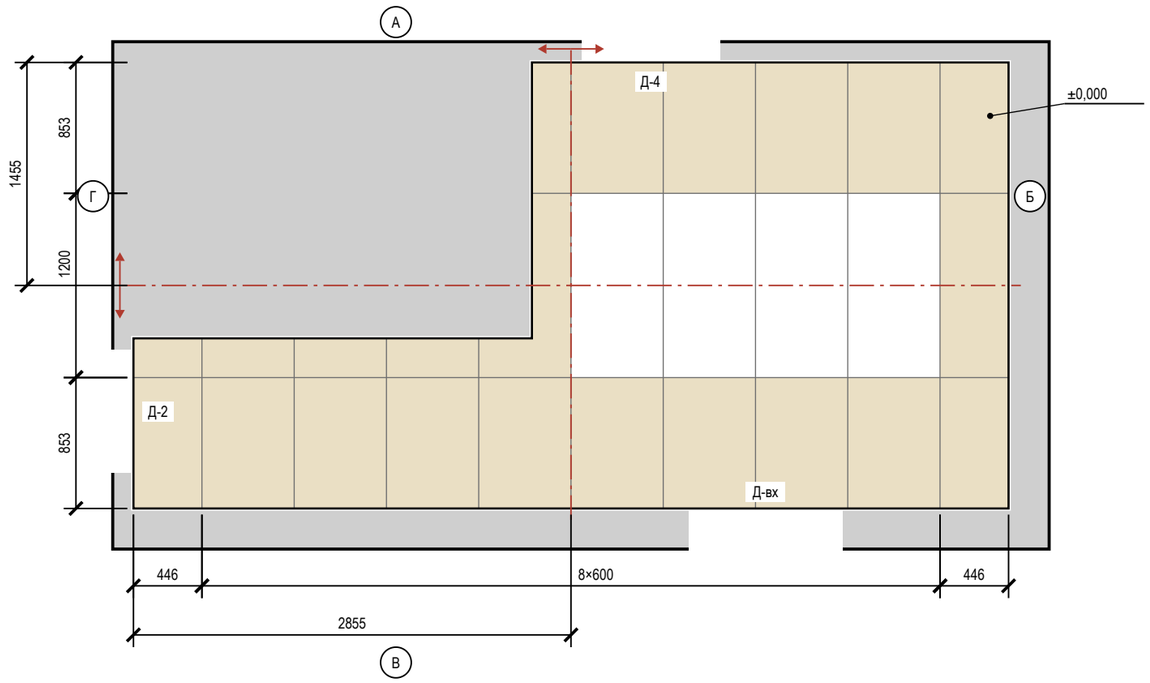

Фрагмент 2. Гостиная-кухня (пом. 1), фартук, стена А. 1200×600, шов 2 мм, М 1:40

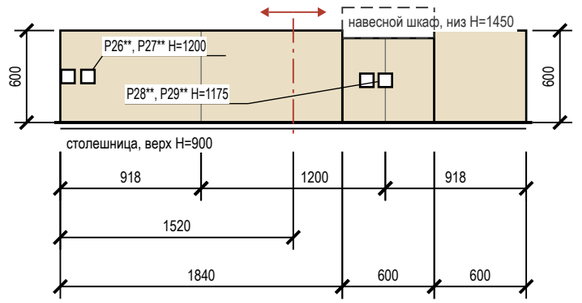

Фрагмент 3. Гостиная-кухня (пом. 1), фартук, стена Б. 1200×600, шов 2 мм, М 1:40

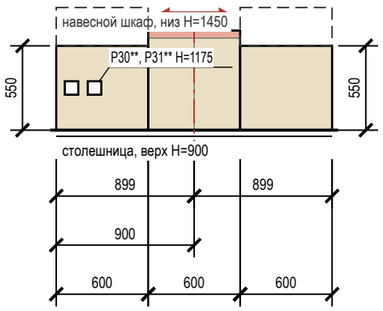

Условные обозначения

- плитка целая; тонкая линия — шов
- плитка с подрезкой (размер — на цепочке)
- ось старта; стрелки — направление укладки
- электроточка: марка и H — по листам ЭОМ
- столешница (верх)
- навесной шкаф над фартуком
- отметка чистого пола на полке выноски, м
- А — обозначение стены А–Г (как на развёртках)

Подсчёт плитки

Поверхность	Формат	S, м²	Целых	Подр.	С запасом
Прихожая, пол	600×1200	12,20	4	22	29
Гостиная-кухня, фартук (ст. А)	1200×600	0,89	0	3	4
Гостиная-кухня, фартук (ст. Б)	1200×600	1,05	0	4	5

Примечания

1. Прихожая: керамогранит 600×1200, длинная сторона — вдоль стен Б и Г, шов 2 мм, прямая раскладка от центра. Стены окрашены: раскладка от чистового контура минус штукатурка и шпаклёвка 15 мм на сторону (принято); подрезки 446 / 853 мм, срез — под плинтус.
2. Прихожая: деформационный зазор по периметру 8–10 мм под плинтусом; в проёмах — стык с соседним покрытием по оси полотна двери. Клей C2 TE S1, затирка CG2WA.
3. Фартук, Гостиная-кухня: 1200×600 горизонтально, шов 2 мм; зоны 1840 мм — 900…1500, 600 мм — 900…1450, 600 мм — 900…1500 (от столешницы до низа навесного шкафа, без шкафа — 600 мм). Старт от центра участка, подрезки 918 мм. Площадь 0,89 м² — как в ведомости отделки.
4. Фартук — после монтажа столешницы, низ на 2–3 мм выше неё, шов со столешницей — санитарный герметик; навесные шкафы — после фартука. Торцы у пенала и стены — профиль или запил 45°.
5. Фартук, Гостиная-кухня: 1200×600 горизонтально, шов 2 мм; зоны 600 мм — 900…1450, 600 мм — 900…1550, 600 мм — 900…1450 (от столешницы до низа навесного шкафа, без шкафа — 650 мм). Старт от центра участка, подрезки 899 мм. Площадь 1,05 м² — как в ведомости отделки.
6. Фартук — после монтажа столешницы, низ на 2–3 мм выше неё, шов со столешницей — санитарный герметик; навесные шкафы — после фартука. Торцы у пенала и стены — профиль или запил 45°.
7. Фартук, Гостиная-кухня: в зоне до отм. 1550 верхний ряд подрезан 48 мм — меньше 1/3 плитки; полоса прикрыта корпусом навесного модуля и на виду не остаётся. Раскладкой не снимается: убрать подрезку можно, только выровняв низ этого модуля с соседними (1450 мм) — решение мебельщика.
8. Клей, затирка и итог по форматам — в ведомостях листа «Раскладка плитки. Планы полов».

Допущения и предложения на листе

Основа листа: взаимное расположение помещений, контур дома 9600 × 8000 и раскладка этажей подобраны проектировщиком под габариты помещений брифа; обмер и проект АР — задание (К-1); высота потолка 2900 мм — по брифу, не замерена; перекрытие 330 мм и отметка 2-го этажа +3,230 приняты; проект КР — задание (К-2); наружные стены 400 мм, перегородки 120 мм приняты (в брифе толщин нет) (К-1); разрешённая мощность 15 кВт принята по типовым ТУ для частного дома (К-4); подрайон климата не задан — принят не северный (жилые от 2,5 м) (К-7).

Знак «**» — предложение проектировщика, заказчиком не утверждено (согласовать с заказчиком): P26, P27 — Сдвиг под раскладку плитки фартука (стена А) на 100 мм выше — ось на шве или в центре плитки, привязка по таблице листа; P28 — Сдвиг под раскладку плитки фартука (стена А) на 75 мм выше — ось на шве или в центре плитки, привязка по таблице листа; P29 — Сдвиг под раскладку плитки фартука (стена А) на 29 мм вдоль стены и на 75 мм выше — ось на шве или в центре плитки, привязка по таблице листа; P30, P31 — Сдвиг под раскладку плитки фартука (стена Б) на 75 мм выше — ось на шве или в центре плитки, привязка по таблице листа; плинтус пом. 1, 5, фартук пом. 1 — артикул изделия не выбран: позиция описана характеристиками («аналог по характеристикам»), артикул выбирается при закупке.

См. лист открытых вопросов (лист 7, записи К-1, К-2, К-4; лист 8, запись К-7).

1000 мм · печать 1:1

Изм.	Кол.уч	Лист	№ док.	Подп.	Дата
Разраб.		Кырлан А.С.			04.11.26
Пров.					
ГИП					
Н. контр.					
Утв.					

ГД-2026-012-АИ

Дом 120 м²

Общая площадь 147,36* м² · * размеры приняты, не замерены (реестр — л. 7–9, К-1)

Дизайн-проект интерьера

Стадия	Лист	Листов
РП	75	175

Раскладка плитки. Прихожая. Фартук кухни

М 1:40


Кырлан Александр Сергеевич

выпуск 04.11.2026 № 4dfa962484 · стр. 77 из 180

Раскладка плитки. Санузел гостевой. Развёртки стен

ПРЕДВАРИТЕЛЬНО · не для производства работ · открыто пунктов: 11 (реестр — л. 7–9)

Пом. 4 · вид изнутри помещения · размеры в мм · высоты от чистого пола, отметки от ±0,000 (чистый пол 1-го этажа)

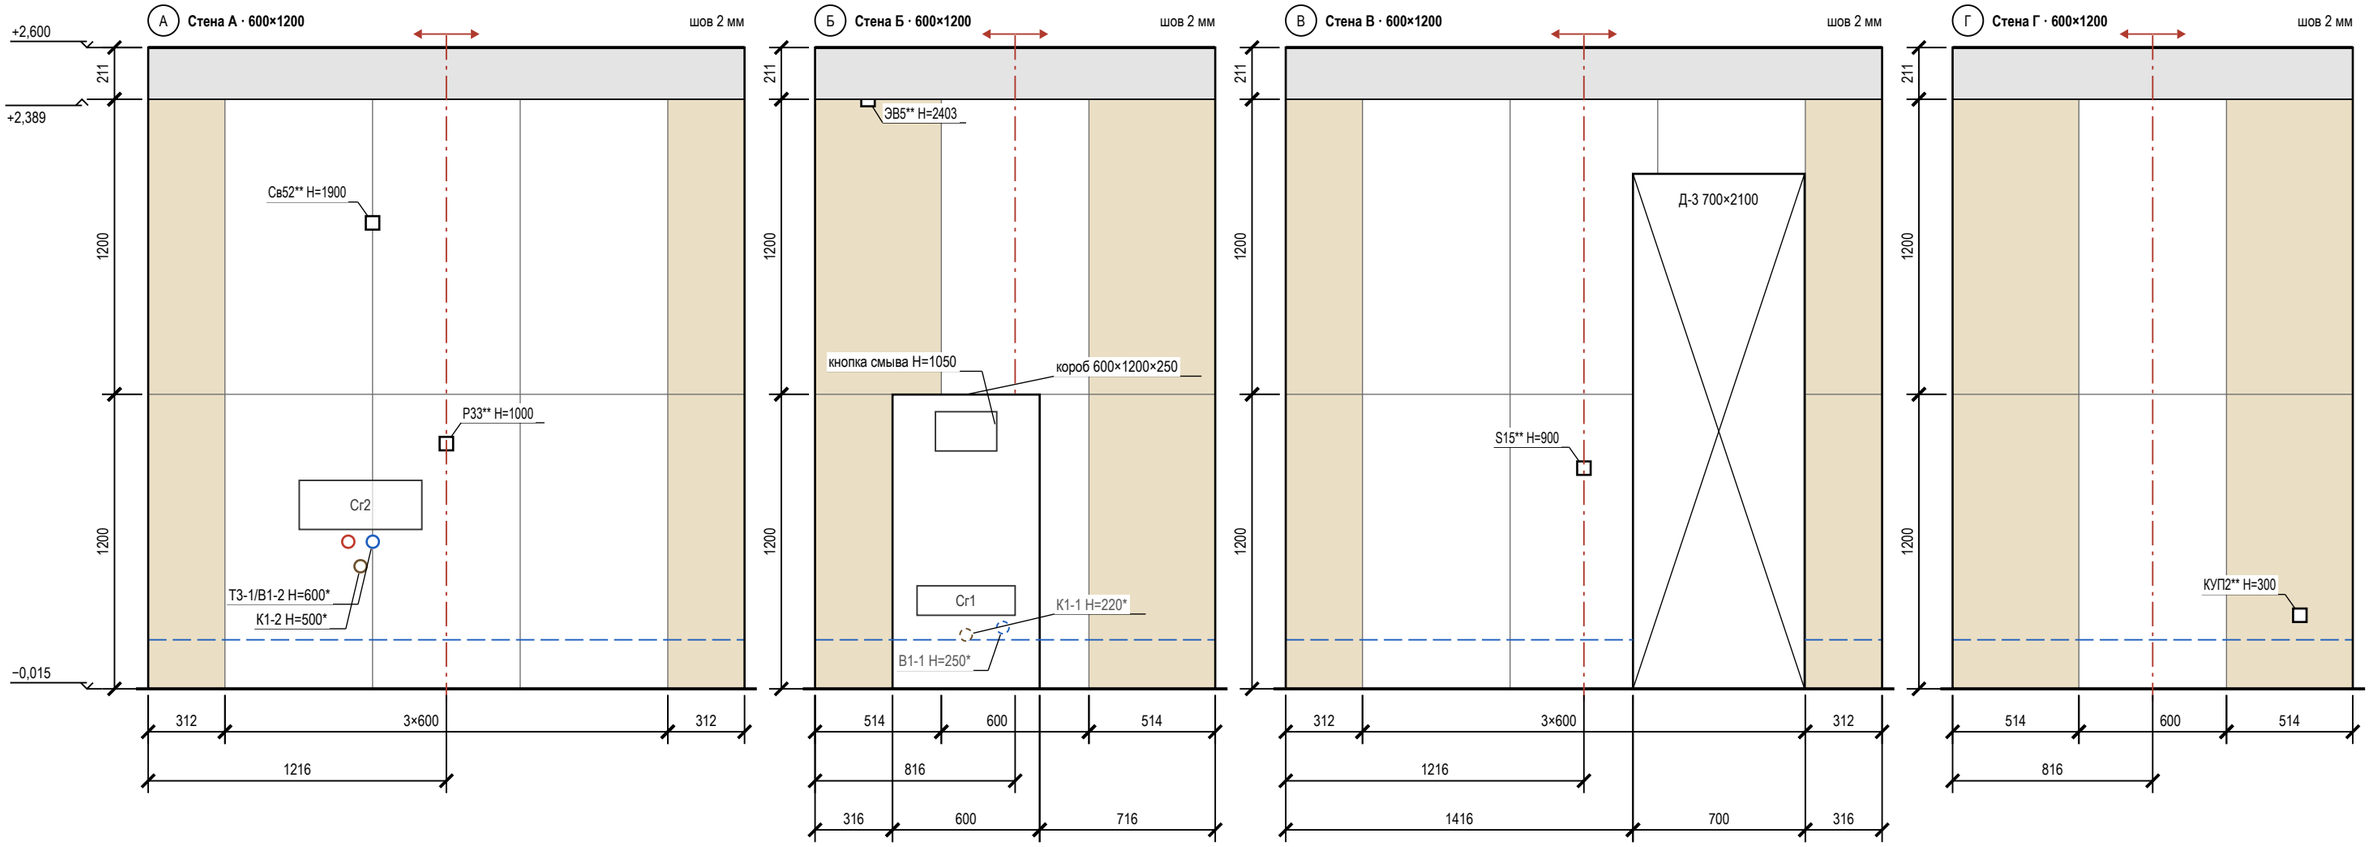

Подсчёт плитки по стенам и коробу

Поверхность	L × H, мм	S, м²	Целых	Подр.	С запасом	Подрезки: край / верх, мм
стена А	2432 × 2404	5,96	6	4	11	312 / 312; целый ряд
стена Б	1632 × 2404	3,32	1	5	7	514 / 514; целый ряд
короб (ст. Б)	600×1200×250	1,47	1	3	5	лицо 600; бок. 250
стена В	2432 × 2404	4,49	2	8	11	312 / 312; целый ряд
стена Г	1632 × 2404	2,90	2	4	7	514 / 514; целый ряд
Итого		**18,15**	**12**	**24**	**41**	

Условные обозначения

- плитка целая; тонкая линия — шов
- плитка с подрезкой (размер — на цепочке)
- ось старта; стрелки — направление укладки
- верх гидроизоляции: 200 от ЧП, в мокрой зоне — «до …»
- проём — не облицовывается
- сантехприбор: габарит, высота по практике
- короб инсталляции, в нём кнопка смыва 250×160
- вывод В1 (код — в ведомости привязок)
- вывод Т3 (код — в ведомости привязок)
- вывод К1 (код — в ведомости привязок)
- вывод за прибором / в коробе (не на сетке)
- электроточка: марка и Н — по листам ЭОМ
- отметка уровня, м: ±0,000 — чистый пол 1-го этажа
- низ потолка; серая полоса — стена без плитки
- (А) обозначение стены А–Г (как на развёртках)

Допущения и предложения на листе. Основа листа: взаимное расположение помещений, контур дома 9600 × 8000 и раскладка этажей подобраны проектировщиком под габариты помещений брифа; обмер и проект АР — задание (К-1); высота потолка 2900 мм — по брифу, не замерена; перекрытие 330 мм и отметка 2-го этажа +3,230 приняты; проект КР — задание (К-2); наружные стены 400 мм, перегородки 120 мм приняты (в брифе толщин нет) (К-1); разрешённая мощность 15 кВт принята по типовым ТУ для частного дома (К-4); подрайон климата не задан — принят не северный (жилые от 2,5 м) (К-7). Знак «*» — принято, не замерено (замерить): К-1: дверь пом. 4 (стена В). Знак «**» — предложено, не утверждено (согласовать): пол пом. 4, Св52, ЭВ5, КУП2, S15; ИЗ-2: Р33. См. лист открытых вопросов (лист 7, записи К-1, К-2, К-4; лист 8, запись К-7; лист 9, запись ИЗ-2).

Примечания

1. Вид изнутри, стены по часовой стрелке А → Г. Высоты — от чистого пола (−0,015), отметки — от ±0,000 (чистый пол 1-го этажа). Раскладка от чистовых размеров (штукатурка 10 + клей 5 + плитка 9 мм), подрезки чистые; старт — от оси стены, ряды от пола целыми.
2. Облицовка не до потолка: верх плитки +2,389, выше — отделка стены по ведомости отделки до потолка +2,600; торец облицовки — профиль-окантовка.
3. Открытые выводы и электроточки — на шве или в центре плитки (допуск 10 мм; плитка от 900 мм по высоте — на шве или не ближе 60 мм к нему).
4. Выводы ВК стоят по оси прибора и с прибором не двигаются — привязки по «Плану выводов сантехники» без сдвига; вне сетки (Т3-1/В1-2, К1-2) — отверстие в плитке коронкой по той же привязке, плитку не сдвигать.
5. Выводы — по «Плану выводов сантехники», электроточки — по ЭОМ, «*» — высота по практике; за приборами и в коробе (В1-1, К1-1) — штриховым кольцом.
6. Гидроизоляция: 200 мм от ЧП по периметру; углы — лентой; акт скрытых работ, пролив.
7. Короб 600×1200×250: лицо 600 мм от оси кнопки смыва, боковины, полка; углы — запил 45° или профиль; за коробом плитку не кладут.

1000 мм · печать 1:1

Изм.	Кол.уч	Лист	№ док.	Подп.	Дата
Разраб.		Кырлан А.С.			04.11.26
Пров.					
ГИП					
Н. контр.					
Утв.					

ГД-2026-012-АИ

Дом 120 м²

Общая площадь 147,36* м² · * размеры приняты, не замерены (реестр — л. 7–9, К-1)

Дизайн-проект интерьера

Стадия	Лист	Листов
РП	76	175

Раскладка плитки. Санузел гостевой. Развёртки стен


М 1:25

Кырлан Александр Сергеевич

выпуск 04.11.2026 № 4dfa962484 · стр. 78 из 180

Раскладка плитки. Санузел второго этажа. Развёртки стен

Пом. 13 · вид изнутри помещения · размеры в мм · высоты от чистого пола, отметки от ±0,000 (чистый пол 1-го этажа)

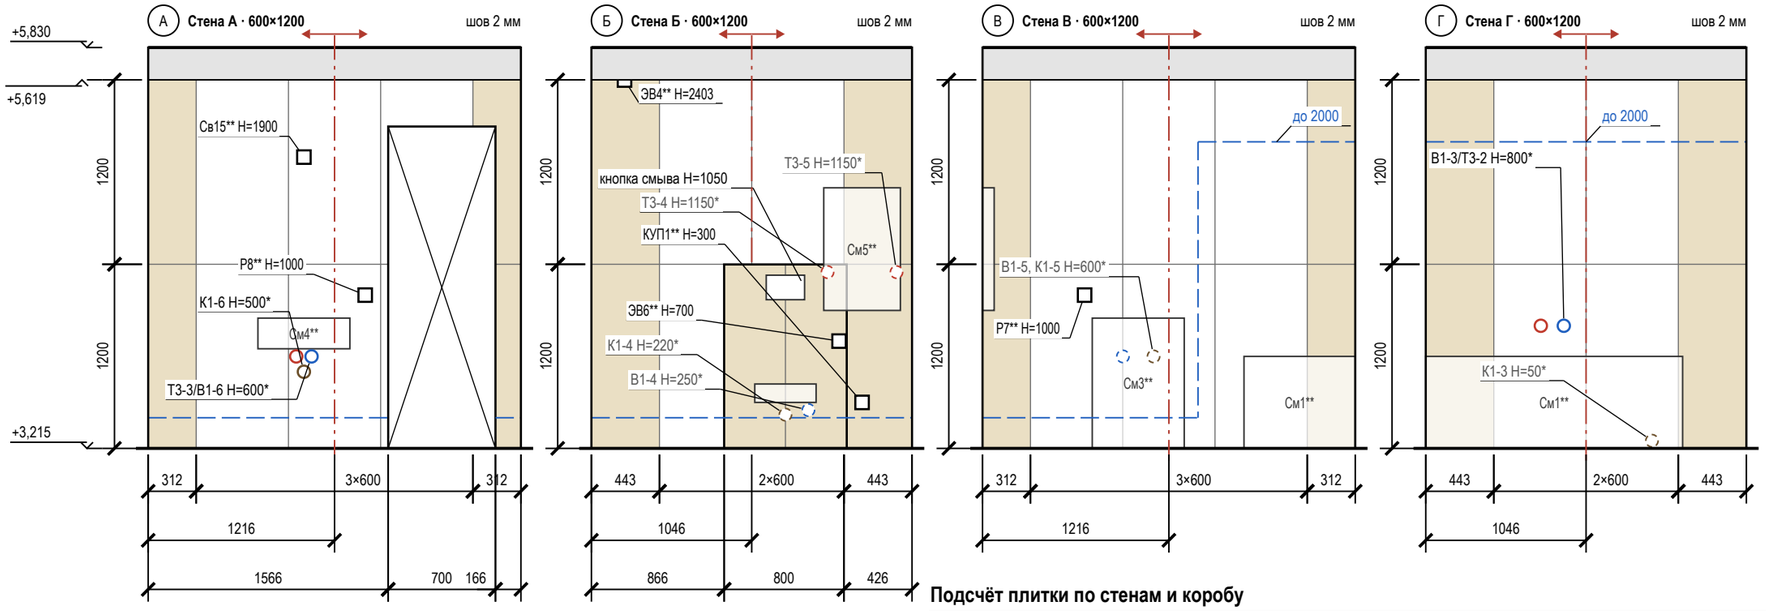

Подсчёт плитки по стенам и коробу

Поверхность	L × H, мм	S, м²	Целых	Подр.	С запасом	Подрезки: край / верх, мм
стена А	2432 × 2404	4,49	4	6	11	312 / 312; целый ряд
стена Б	2092 × 2404	4,18	2	5	8	443 / 443; целый ряд
короб (ст. Б)	800×1200×250	1,76	0	6	7	лицо 399 / 399; бок. 250
стена В	2432 × 2404	5,96	6	4	11	312 / 312; целый ряд
стена Г	2092 × 2404	3,46	4	4	9	443 / 443; целый ряд
Итого		**19,86**	**16**	**25**	**46**	

Сдвиг точек под раскладку

Точка (ВК, ЭОМ)	Стена	Проект: от угла / H	Под раскладку: от угла / H	Сдвиг, мм
Р8**	А	1416 / 1000	1517 / 1000	+101 на шов
Св15**	А	1016 / 1900	915 / 1900	−101 на шов
ЭВ4**	Б	216 / 2403	143 / 2403	−73 в центр плитки
КУП1**	Б	1766 / 300	1648 / 300	−118 на шов
ЭВ6**	Б	1616 / 700	1648 / 700	+32 на шов
Р7**	В	666 / 1000	614 / 1000	−52 в центр плитки

Условные обозначения

- плитка целая; тонкая линия — шов
- плитка с подрезкой (размер — на цепочке)
- ось старта; стрелки — направление укладки
- верх гидроизоляции: 200 от ЧП, в мокрой зоне — «до …»
- проём — не облицовывается
- сантехприбор: габарит, высота по практике
- короб инсталляции, в нём кнопка смыва 250×160
- вывод В1 (код — в ведомости привязок)
- вывод Т3 (код — в ведомости привязок)
- вывод К1 (код — в ведомости привязок)
- вывод за прибором / в коробе (не на сетке)
- электроточка: марка и H — по листам ЭОМ
- отметка уровня, м: ±0,000 — чистый пол 1-го этажа
- низ потолка; серая полоса — стена без плитки
- (А) обозначение стены А–Г (как на развёртках)

Допущения и предложения на листе

Основа листа: взаимное расположение помещений, контур дома 9600 × 8000 и раскладка этажей подобраны проектировщиком под габариты помещений брифа; обмер и проект АР — задание (К-1); высота потолка 2900 мм — по брифу, не замерена; перекрытие 330 мм и отметка 2-го этажа +3,230 приняты; проект КР — задание (К-2); наружные стены 400 мм, перегородки 120 мм приняты (в брифе толщин нет) (К-1); разрешённая мощность 15 кВт принята по типовым ТУ для частного дома (К-4); подрайон климата не задан — принят не северный (жилые от 2,5 м) (К-7).

Знак «*» — принято, не замерено и не подтверждено (замерить на объекте): К-1: дверь пом. 13 (стена А) — Петли у правого откоса (х 6150, у стояков): открытое полотно стоит вдоль стены Б, вошедший идёт влево к умывальнику и ванне; К-2: отметка чистого пола этажа «2-й этаж» +3,230 — отметка чистого пола 2-го этажа +3,230 принята: высота потолка 2900 по брифу + перекрытие с полом 330 (конструкция перекрытия не задана; проект КР — задание).

Знак «**» — предложение проектировщика, заказчиком не утверждено (согласовать с заказчиком): ЭВ4 — Вентилятор ВР1 на стене Б у потолка, offset 300 (над зоной входа); пол пом. 13 — пирог пола: стяжка 33 мм и обмазочная гидроизоляция добавлены разработчиком проекта; артикул изделия не выбран: позиция описана характеристиками («аналог по характеристикам»), артикул выбирается при закупке; ИЗ-1: См1 — Было у стены В offset 150 — заходила в полосу 600 мм перед проёмом Д-8 и в зону 750 перед машиной См3; См3 — Было у стены Г offset 300 — пересекалась с умывальником См4 в углу А/Г, люк упирался в раковину; См5 — Было у стены Г offset 1000 — в 2,3 м от стояка ГВС и в полосе перед проёмом; Св15 — Бра над умывальником См4 — по оси раковины (offset 1100); КУП1 — КУП за унитазом См2 (1150…1550) ниже — offset 1850, H=300; ИЗ-1, ИЗ-2: Р7 — Розетка стиральной машины — за машиной См3 (стена В, 1200…1800), H=1000, вне зон 0–2 ванны (ванна у стены Г до х 4550); Р8 — Фен у умывальника См4 (800…1400 на стене А): справа от раковины, до откоса проёма Д-8 (1650) — 150 мм; ЭВ6 — Вывод полотенцесушителя См5 (стена Б, 1600…2100); К-9: См4 — Было offset 500…1100 — пересекалась со стиральной машиной См3.

Изменения по листу без подписи: ИЗ-1.

См. лист открытых вопросов (лист 7, записи К-1, К-2, К-4; лист 8, записи К-7, К-9; лист 9, записи ИЗ-1, ИЗ-2).

Примечания

1. Вид изнутри, стены по часовой стрелке А → Г. Высоты — от чистого пола (+3,215), отметки — от ±0,000 (чистый пол 1-го этажа). Раскладка от чистовых размеров (штукатурка 10 + клей 5 + плитка 9 мм), подрезки чистые; старт — от оси стены, ряды от пола целыми.
2. Облицовка не до потолка: верх плитки +5,619, выше — отделка стены по ведомости отделки до потолка +5,830; торец облицовки — профиль-окантовка.
3. Точки из таблицы сдвигов переносятся до черновой разводки (ЭОМ — по тем же числам).
4. Выводы ВК стоят по оси прибора и с прибором не двигаются — привязки по «Плану выводов сантехники» без сдвига; вне сетки (Т3-3/В1-6, К1-6, В1-3/Т3-2) отверстие в плитке коронкой по той же привязке, плитку не сдвигать.
5. Выводы — по «Плану выводов сантехники», электроточки — по ЭОМ, «*» — высота по практике; за приборами и в коробе (В1-4, К1-4, Т3-4, Т3-5, В1-5, К1-5, К1-3) — штриховым кольцом.
6. Гидроизоляция: 200 мм от ЧП по периметру; над ванной — до 2000 и 300 мм за борт (СП 29.13330.2011, п. 7.2 — на высоту замачивания); углы — лентой; акт скрытых работ, пролив.
7. Короб 800×1200×250: лицо 399 / 399 мм от оси кнопки смыва, боковины, полка; углы — запил 45° или профиль; за коробом плитку не кладут.
8. Короб заходит на См5** на 150 мм: сузить до 500 мм или сдвинуть прибор (решение дизайнера до закупки).

1000 мм · печать 1:1

Изм.	Кол.уч	Лист	№ док.	Подп.	Дата
Разраб.		Кырлан А.С.			04.11.26
Пров.					
ГИП					
Н. контр.					
Утв.					

ГД-2026-012-АИ

Дом 120 м²

Общая площадь 147,36* м² · * размеры приняты, не замерены (реестр — л. 7–9, К-1)

Дизайн-проект интерьера

Стадия	Лист	Листов
РП	77	175

Раскладка плитки. Санузел второго этажа. Развёртки стен

М 1:40

Кырлан Александр Сергеевич

выпуск 04.11.2026 № 4dfa962484 · стр. 79 из 180

План полов · 1-й этаж

Покрытия, направление укладки, отметки чистого пола, стыки · размеры в мм · отметки в м


ПРЕДВАРИТЕЛЬНО · не для производства работ · открыто пунктов: 11 (реестр — л. 7–9)

Условные обозначения

- тип 1 — инженерная доска, линии — вдоль доски
- тип 2 — керамогранит 600×600, сетка — формат плитки
- тип 3 — керамогранит 600×1200, сетка — формат плитки
- 1 — номер типа пола (экспликация полов)
- схема пола, без масштаба: плита — штриховка, стяжка — точки, звукоизоляция — зигзаг, гидроизоляция — утолщённая линия с заведением на стену
- направление укладки (длинная сторона доски)
- отметка чистого пола, м
- стык в проёме: решение не задано
- стык в проёме: порог
- СТ1 — марка стыка (ведомость стыков)
- стояк: К1 — канализация, В1 ХВС, Т3 — ГВС
- 1 — номер помещения, площадь м²

Отметки по высоте

±0,000	чистый пол пом. 1–3, 5; отсчёт высот
−0,015	чистый пол пом. 4, ниже на 15 мм
−0,064*	верх плиты — расчёт, не замер (задание на обмер)
сущ. пол	снимается до плиты; не замерен (задание на обмер)

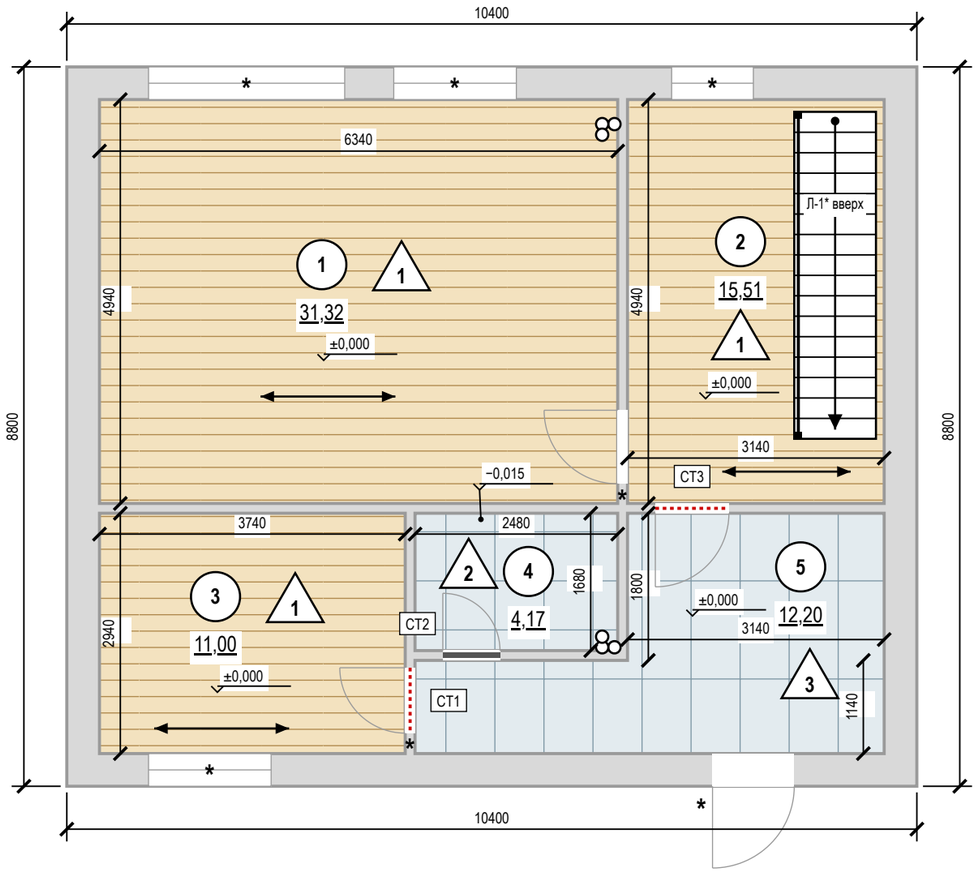

Допущения и предложения на листе. Основа листа: взаимное расположение помещений, контур дома 9600 × 8000 и раскладка этажей подобраны проектировщиком под габариты помещений брифа; обмер и проект АР — задание (К-1); высота потолка 2900 мм — по брифу, не замерена; перекрытие 330 мм и отметка 2-го этажа +3,230 приняты; проект КР — задание (К-2); наружные стены 400 мм, перегородки 120 мм приняты (в брифе толщин нет) (К-1); разрешённая мощность 15 кВт принята по типовым ТУ для частного дома (К-4); подрайон климата не задан — принят не северный (жилые от 2,5 м) (К-7). Знак «*» — принято, не замерено и не подтверждено (замерить на объекте): К-1: дверь пом. 4 (стена В), 5 (А) — проём: место и ширина приняты проектировщиком по брифу (раскладка этажей — К-1), не замерены; К-3: Л-1 — место, тип и размеры лестницы брифом не заданы (только «лестница из холла 1-го этажа»): одномаршевая 17 × 190 × 250 вдоль стены Б холла — предложение проектировщика; конструкция и расчёт — проект КР; К-5: Ст К1-1, Ст В1-1, Ст Т3-1, Ст К1-2 (кухня), Ст В1-2, Ст Т3-2 — положение стояка принято проектировщиком (проект ВК дома не передан), не замерено. Знак «**» — предложение проектировщика, заказчиком не утверждено (согласовать с заказчиком): плинтус пом. 1–3, 5, фартук пом. 1 — артикул изделия не выбран: позиция описана характеристиками («аналог по характеристикам»), артикул выбирается при закупке; пол пом. 4 — пирог пола: стяжка 33 мм и обмазочная гидроизоляция добавлены разработчиком проекта; артикул изделия не выбран: позиция описана характеристиками («аналог по характеристикам»), артикул выбирается при закупке. См. лист открытых вопросов (лист 7, записи К-1–К-5; лист 8, запись К-7).

Примечания

1. За отметку ±0,000 принят чистый пол 1-го этажа, не существующий (блок отметок). Площади — по чистым размерам помещений, м²; размеры — в мм.
2. Стык разнотипных покрытий — по оси дверного полотна (под полотном в закрытом положении); решение стыка — по ведомости стыков.
3. Размеры помещений в свету (ширина × длина, мм), не поместившиеся на плане: пом. 5 — 3140 × 1800, 5740 × 1140.
4. Пол санузлов ниже смежных помещений на 15 мм за счёт меньшей толщины стяжки (верх плиты общий — по экспликации полов); гидроизоляция по стяжке с заведением на стены не менее 200 мм (СП 29.13330.2011, п. 7.2), до облицовки — тест проливом и акт скрытых работ.
5. Трубопроводы в конструкции пола не прокладываются: пирог пола 49–64 мм не вмещает выпуски канализации с уклоном — выпуски К1 ведутся по стенам над чистым полом в коробах.
6. Штучные покрытия (инженерная доска): направление — по стрелке; влажность основания по СМ не более 2,0 % (по ТУ изготовителя).
7. Ровность основания — просвет под 2-метровой рейкой не более 2 мм: пом. 1, 2, 3 (инженерная доска), пом. 4, 5 (керамогранит); проверить до укладки покрытия (СП 71.13330.2017, табл. 8.5).
8. Сетка на плитке — условная, в размер формата; точка старта и раскладка — по листу раскладки плитки.
9. Узор покрытия (заливка-код типа пола) прерывается под надписями — площадями помещений и отметками чистого пола.
10. Пироги полов — по экспликации полов: слои сверху вниз, толщины в мм; гидроизоляция мокрых зон — в пироге и в ведомости отделки; схема пола — без масштаба.

1000 мм · печать 1:1

Экспликация полов

Пом.	Тип пола	Схема пола	Данные элементов пола (наименование, толщина, основание), мм	Площадь, м²
1, 2, 3	1		Инженерная доска на клею — 14 Стяжка ЦПС М200 — 50 Плита перекрытия Всего 64 мм; ЧП ±0,000, верх плиты −0,064	57,83
4	2		Керамогранит на клею С2 TE S1 14 Гидроизоляция обмазочная, 2 слоя, с заведением на стены 200 мм — 2 Стяжка ЦПС М200 — 33 Плита перекрытия Всего 49 мм; ЧП −0,015, верх плиты −0,064	4,17
5	3		Керамогранит на клею С2 TE S1 14 Стяжка ЦПС М200 — 50 Плита перекрытия Всего 64 мм; ЧП ±0,000, верх плиты −0,064	12,20
			Итого	**74,20**

Раскладка покрытий

Пом.	Укладка	Старт (оси от чистовых стен), мм	Отступ 1-го ряда / крайние плитки, мм
1	вдоль стен А/В, прямая	от стены А, 1-й ряд вдоль неё	зазор от стены не задан
2	вдоль стен А/В, прямая	от стены А, 1-й ряд вдоль неё	зазор от стены не задан
3	вдоль стен А/В, прямая	от стены В, 1-й ряд вдоль неё	зазор от стены не задан
4	прямая, сетка 600×600, шов 2	ось X 1216 от Г; ось Y 816 от А	X 312 / 312; Y 514 / 514
5	плитка	раскладка плиточника не задана	

Стыки покрытий в проёмах

Марка	Проём	Типы пола	Отметки ЧП	Решение
СТ1	3–5 (Д-2)	1 / 3	±0,000 / ±0,000	не задано
СТ2	4–5 (Д-3)	2 / 3	−0,015 / ±0,000	порог h=15 мм
СТ3	5–2 (Д-4)	3 / 1	±0,000 / ±0,000	не задано

Изм.	Кол.уч	Лист	№ док.	Подп.	Дата
Разраб.		Кырлан А.С.			04.11.26
Пров.					
ГИП					
Н. контр.					
Утв.					

ГД-2026-012-АИ

Дом 120 м²

Общая площадь 147,36* м² · * размеры приняты, не замерены (реестр — л. 7–9, К-1)

Дизайн-проект интерьера

Стадия	Лист	Листов
РП	78	175

План полов · 1-й этаж

М 1:75

Кырлан Александр Сергеевич

выпуск 04.11.2026 № 4dfa962484 · стр. 80 из 180

План полов · 2-й этаж

Покрытия, направление укладки, отметки чистого пола, стыки · размеры в мм · отметки в м


ПРЕДВАРИТЕЛЬНО · не для производства работ · открыто пунктов: 11 (реестр — л. 7–9)

Условные обозначения



- тип 1 — инженерная доска, линии — вдоль доски
- тип 2 — керамогранит 600×600, сетка — формат плитки
- 1 — номер типа пола (экспликация полов)
- схема пола, без масштаба: плита — штриховка, стяжка — точки, звукоизоляция — зигзаг, гидроизоляция — утолщённая линия с заведением на стену
- направление укладки (длинная сторона доски)
- отметка чистого пола, м
- стык в проёме: без порога (б/п)
- стык в проёме: порог
- СТ1 — марка стыка (ведомость стыков)
- стояк: К1 — канализация, В1 ХВС, Т3 — ГВС
- (1) — номер помещения, площадь м²

Отметки по высоте

±0,000	чистый пол 1-го этажа; отсчёт отметок
+3,230*	чистый пол пом. 6–12 (2-й этаж)
+3,215*	чистый пол пом. 13, ниже на 15 мм
+3,166*	верх плиты — расчёт, не замер (задание на обмер)
сущ. пол	снимается до плиты; не замерен (задание на обмер)

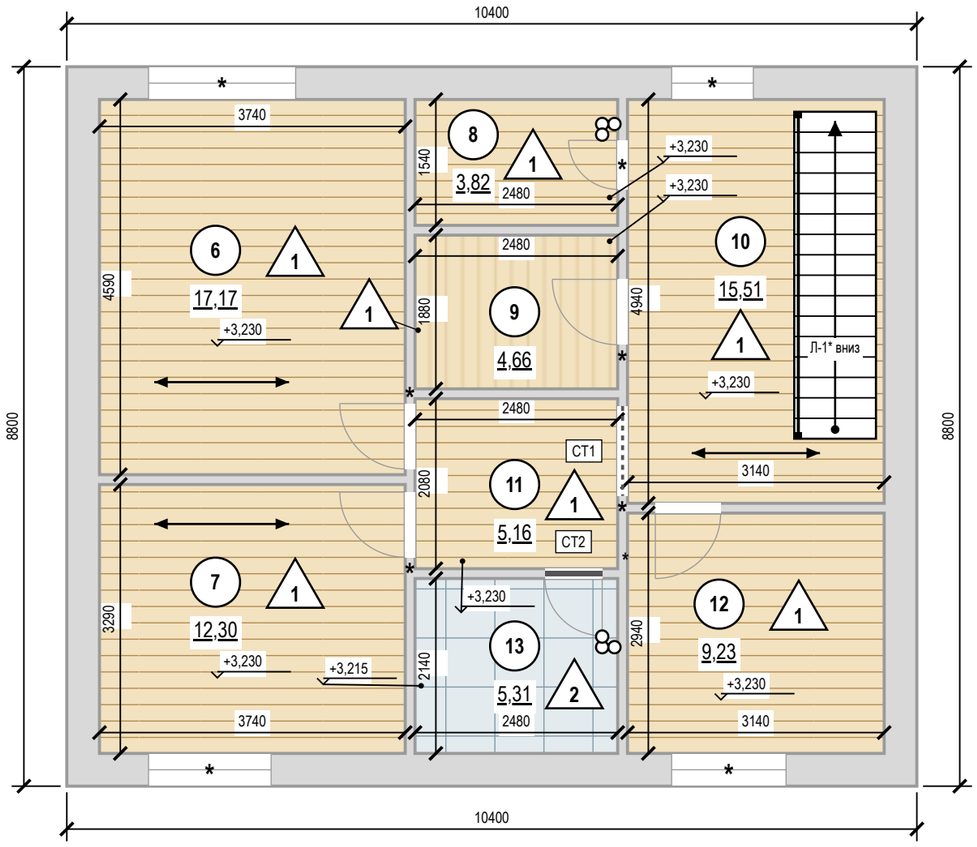

Экспликация полов

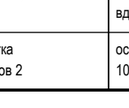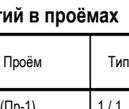Пом.	Тип пола	Схема пола	Данные элементов пола (наименование, толщина, основание), мм	Площадь, м²
6, 7, 8, 9, 10, 11, 12	1		Инженерная доска на клею — 14 Стяжка ЦПС М200 — 50 Плита перекрытия Всего 64 мм; ЧП +3,230, верх плиты +3,166	67,85
13	2		Керамогранит на клею C2 TE S1 14 Гидроизоляция обмазочная, 2 слоя, с заведением на стены 200 мм — 2 Стяжка ЦПС М200 — 33 Плита перекрытия Всего 49 мм; ЧП +3,215, верх плиты +3,166	5,31
			Итого	**73,16**

Раскладка покрытий

Пом.	Укладка	Старт (оси от чистовых стен), мм	Отступ 1-го ряда / крайние плитки, мм
6	вдоль стен А/В, прямая	от стены А, 1-й ряд вдоль неё	зазор от стены не задан
7	вдоль стен А/В, прямая	от стены В, 1-й ряд вдоль неё	зазор от стены не задан
8	вдоль стен А/В, прямая	от стены А, 1-й ряд вдоль неё	зазор от стены не задан
9	вдоль стен Б/Г, прямая	от стены Г, 1-й ряд вдоль неё	зазор от стены не задан
10	вдоль стен А/В, прямая	от стены А, 1-й ряд вдоль неё	зазор от стены не задан
11	вдоль стен А/В, прямая	от стены А, 1-й ряд вдоль неё	зазор от стены не задан
12	вдоль стен А/В, прямая	от стены В, 1-й ряд вдоль неё	зазор от стены не задан
13	прямая, сетка 600×600, шов 2	ось X 1216 от Г; ось Y 1046 от А	X 312 / 312; Y 443 / 443

Стыки покрытий в проёмах

Марка	Проём	Типы пола	Отметки ЧП	Решение
СТ1	11–10 (Пр-1)	1 / 1	+3,230 / +3,230	б/п
СТ2	13–11 (Д-8)	2 / 1	+3,215 / +3,230	порог h=15 мм

Допущения и предложения на листе. Основа листа: взаимное расположение помещений, контур дома 9600 × 8000 и раскладка этажей подобраны проектировщиком под габариты помещений брифа; обмер и проект АР — задание (К-1); высота потолка 2900 мм — по брифу, не замерена; перекрытие 330 мм и отметка 2-го этажа +3,230 приняты; проект КР — задание (К-2); наружные стены 400 мм, перегородки 120 мм приняты (в брифе толщин нет) (К-1); разрешённая мощность 15 кВт принята по типовым ТУ для частного дома (К-4); подрайон климата не задан — принят не северный (жилые от 2,5 м) (К-7). Знак «*» — принято, не замерено (замерить): К-1: дверь пом. 12 (стена А); К-2: отметка чистого пола этажа «2-й этаж» +3,230; К-3: Л-1; К-5: Ст К1-1, Ст В1-1, Ст Т3-1, Ст К1-2 (кухня), Ст В1-2, Ст Т3-2. Знак «**» — предложено, не утверждено (согласовать): плинтус пом. 6, 8, 10, 11, пол пом. 13. См. лист открытых вопросов (лист 7, записи К-1–К-5; лист 8, запись К-7).

Примечания

1. За отметку ±0,000 принят чистый пол 1-го этажа, не существующий; чистый пол этажа +3,230 (блок отметок). Площади — по чистым размерам помещений, м²; размеры — в мм.
2. Стык разнотипных покрытий — по оси дверного полотна (под полотном в закрытом положении); решение стыка — по ведомости стыков.
3. Пол санузлов ниже смежных помещений на 15 мм за счёт меньшей толщины стяжки (верх плиты общий — по экспликации полов); гидроизоляция по стяжке с заведением на стены не менее 200 мм (СП 29.13330.2011, п. 7.2), до облицовки — тест проливом и акт скрытых работ.
4. Трубопроводы в конструкции пола не прокладываются: пирог пола 49–64 мм не вмещает выпуски канализации с уклоном — выпуски К1 ведутся по стенам над чистым полом в коробах.
5. Штучные покрытия (инженерная доска): направление — по стрелке; влажность основания по СМ не более 2,0 % (по ТУ изготовителя).
6. Ровность основания — просвет под 2-метровой рейкой не более 2 мм: пом. 6, 7, 8, 9, 10, 11, 12 (инженерная доска), пом. 13 (керамогранит); проверить до укладки покрытия (СП 71.13330.2017, табл. 8.5).
7. Сетка на плитке — условная, в размер формата; точка старта и раскладка — по листу раскладки плитки.
8. Узор покрытия (заливка-код типа пола) прерывается под надписями — площадями помещений и отметками чистого пола.
9. Пироги полов — по экспликации полов: слои сверху вниз, толщины в мм; гидроизоляция мокрых зон — в пироге и в ведомости отделки; схема пола — без масштаба.

1000 мм · печать 1:1

Изм.	Кол.уч	Лист	№ док.	Подп.	Дата
Разраб.		Кырлан А.С.			04.11.26
Пров.					
ГИП					
Н. контр.					
Утв.					

ГД-2026-012-АИ

Дом 120 м²

Общая площадь 147,36* м² · * размеры приняты, не замерены (реестр — л. 7–9, К-1)

Дизайн-проект интерьера

Стадия	Лист	Листов
РП	79	175

План полов · 2-й этаж

М 1:75

Кырлан Александр Сергеевич

выпуск 04.11.2026 № 4dfa962484 · стр. 81 из 180

Ведомость отделки помещений. Лист 1 из 3

ПРЕДВАРИТЕЛЬНО · не для производства работ · открыто пунктов: 11 (реестр — л. 7–9)

Потолки, стены, низ стен, полы · площади в м², длины в м · отметки в м

Ведомость отделки помещений (форма 1 прил. А ГОСТ 21.501-2018). Лист 1 из 3

№	Наименование помещения	Потолок			Стены и перегородки			Низ стен (плинтус)			Пол		Примечание
		Вид отделки	Код цвета	S, м²	Вид отделки	Код цвета	S, м²	Вид отделки	Код цвета	L, м	Вид отделки	S, м²	
1	Гостиная-кухня 31,32 м²	ГКЛ по каркасу П113, отм. +2,700; +2,800; +2,750; окраска, Little Greene Absolute Matt, глубокоматовая, 2 слоя, подготовка Q3	Little Greene No. 222	31,32	Окраска, Tikkurila, матовая, 2 слоя, подготовка Q3 Акцент — стена А: окраска, Tikkurila, матовая, 2 слоя, подготовка Q3 Фартук кухни (стена А, Б): облицовка керамогранитом, аналог: керамогранит под травертин, матовый, 1200×600×9 мм, клей C2 TE S1, затирка CG2WA	Tikkurila G503 NCS S 3050-R80B по артикулу	39,96 10,31 1,94	Плинтус МДФ h=80 мм, аналог: МДФ под покраску 80×16	Tikkurila G503	21,7	Инженерная доска, 1167-4250, 2100×127 мм, на клею; тип 1, отм. ЧП ±0,000	31,32	Н стен 2700 (до потолка); матовая моющаяся, класс 1 EN 13300 — осознанно вместо полуматовой; краска бренда веера G503 — Tikkurila матовая линейка класса 1 — по каталогу Tikkurila при закупке; краска бренда веера Little Greene; класс по EN 13300 и блеск линейки — по ТУ Little Greene, в базе не сверены; плинтус в цвет: стены
2	Холл с лестницей 15,51 м²	ГКЛ по каркасу П113, отм. +2,800; окраска, Little Greene Absolute Matt, глубокоматовая, 2 слоя, подготовка Q3	Little Greene No. 222	15,51	Окраска, Tikkurila, матовая, 2 слоя, подготовка Q3	Tikkurila G503	33,04	Плинтус МДФ h=80 мм, аналог: МДФ под покраску 80×16	Tikkurila G503	11,1	Инженерная доска, 1167-4250, 2100×127 мм, на клею; тип 1, отм. ЧП ±0,000	15,51	Н стен 2800 (до потолка); матовая моющаяся, класс 1 EN 13300 — осознанно вместо полуматовой; краска бренда веера G503 — Tikkurila матовая линейка класса 1 — по каталогу Tikkurila при закупке; краска бренда веера Little Greene; класс по EN 13300 и блеск линейки — по ТУ Little Greene, в базе не сверены; плинтус в цвет: стены
3	Кабинет 11,00 м²	ГКЛ по каркасу П113, отм. +2,800; +2,650; окраска, Little Greene Absolute Matt, глубокоматовая, 2 слоя, подготовка Q3	Little Greene No. 222	11,00	Окраска, Tikkurila, матовая, 2 слоя, подготовка Q3 Акцент — стена А: окраска, Tikkurila, матовая, 2 слоя, подготовка Q3	Tikkurila G503 NCS S 5020-G90Y	23,01 10,47	Плинтус МДФ h=80 мм, аналог: МДФ под покраску 80×16	Tikkurila G503	12,6	Инженерная доска, 1167-4250, 2100×127 мм, на клею; тип 1, отм. ЧП ±0,000	11,00	Н стен 2800 (до потолка); краска бренда веера G503 Tikkurila; матовая линейка класса 1 — по каталогу Tikkurila при закупке; краска бренда веера Little Greene класс по EN 13300 и блеск линейки — по ТУ Little Greene, в базе не сверены; плинтус в цвет: стены
4	Санузел гостевой 4,17 м²	ГКЛВ по каркасу П113, отм. +2,600; окраска, Little Greene Intelligent Bathroom, матовая, 2 слоя, подготовка Q3	Little Greene No. 222	4,17	Облицовка плиткой, A8UZ, 600×1200×9 мм, клей C2 TE S1, затирка CG2WA	Atlas Concorde A8UZ	17,40	нет			Аналог: керамогранит ректифицированный под травертин, матовый, 600×600×9 мм; тип 2, отм. ЧП −0,015	4,17	Н стен 2615 (до потолка); гидроизоляция обмазочная, 2 слоя, с заведением на стены 200 мм (по пирогу пола); тест проливом и акт скрытых работ; краска бренда веера Little Greene; класс по EN 13300 и блеск линейки — по ТУ Little Greene, в базе не сверены

Примечания

1. Ведомость продолжена на листе 2 из 3; итоги, сводка площадей и примечания — на последнем листе ведомости.

Допущения и предложения на листе

Основа листа: взаимное расположение помещений, контур дома 9600 × 8000 и раскладка этажей подобраны проектировщиком под габариты помещений брифа; обмер и проект АР — задание (К-1); высота потолка 2900 мм — по брифу, не замерена; перекрытие 330 мм и отметка 2-го этажа +3,230 приняты; проект КР — задание (К-2); наружные стены 400 мм, перегородки 120 мм приняты (в брифе толщин нет) (К-1); разрешённая мощность 15 кВт принята по типовым ТУ для частного дома (К-4); подрайон климата не задан — принят не северный (жилые от 2,5 м) (К-7).

Знак «**» — предложение проектировщика, заказчиком не утверждено (согласовать с заказчиком): плинтус пом. 1–3, 5, 6, 8, 10, 11, фартук пом. 1 — артикул изделия не выбран: позиция описана характеристиками («аналог по характеристикам»), артикул выбирается при закупке; пол пом. 4, 13 — пирог пола: стяжка 33 мм и обмазочная гидроизоляция добавлены разработчиком проекта; артикул изделия не выбран: позиция описана характеристиками («аналог по характеристикам»), артикул выбирается при закупке.

См. лист открытых вопросов (лист 7, записи К-1, К-2, К-4; лист 8, запись К-7).

Изм.	Кол.уч	Лист	№ док.	Подп.	Дата
Разраб.		Кырлан А.С.			04.11.26
Пров.					
ГИП					
Н. контр.					
Утв.					

ГД-2026-012-АИ

Дом 120 м²

Общая площадь 147,36* м² · * размеры приняты, не замерены (реестр — л. 7–9, К-1)

Дизайн-проект интерьера	Стадия	Лист	Листов
	РП	80	175
Ведомость отделки помещений. Лист 1 из 3 М б/м	**Кырлан Александр Сергеевич**		

выпуск 04.11.2026 № 4dfa962484 · стр. 82 из 180

Ведомость отделки помещений. Лист 2 из 3

ПРЕДВАРИТЕЛЬНО · не для производства работ · открыто пунктов: 11 (реестр — л. 7–9)

Потолки, стены, низ стен, полы · площади в м², длины в м · отметки в м

Ведомость отделки помещений (форма 1 прил. А ГОСТ 21.501-2018). Лист 2 из 3

№	Наименование помещения	Потолок			Стены и перегородки			Низ стен (плинтус)			Пол		Примечание
		Вид отделки	Код цвета	S, м²	Вид отделки	Код цвета	S, м²	Вид отделки	Код цвета	L, м	Вид отделки	S, м²	
5	Прихожая 12,20 м²	ГКЛ по каркасу П113, отм. +2,750; окраска, Little Greene Absolute Matt, глубокоматовая, 2 слоя, подготовка Q3	Little Greene No. 222	12,20	Окраска, Tikkurila, матовая, 2 слоя, подготовка Q3	Tikkurila G503	40,60	Плинтус МДФ h=80 мм, аналог: МДФ под покраску 80×16	Tikkurila G503	14,0	Керамогранит, A8UZ, 600×1200×9 мм; тип 3, отм. ЧП ±0,000	12,20	Н стен 2750 (до потолка); матовая моющаяся, класс 1 EN 13300 — осознанно вместо полуматовой; краска бренда веера G503 — Tikkurila матовая линейка класса 1 — по каталогу Tikkurila при закупке; краска бренда веера Little Greene; класс по EN 13300 и блеск линейки — по ТУ Little Greene, в базе не сверены; плинтус в цвет: стены
6	Спальня родителей 17,17 м²	ГКЛ по каркасу П113, отм. +6,030; +5,880; окраска, Little Greene Absolute Matt, глубокоматовая, 2 слоя, подготовка Q3	Little Greene No. 222	17,17	Окраска, Tikkurila, матовая, 2 слоя, подготовка Q3 Акцент — стена А: окраска, Farrow & Ball Modern Emulsion, матовая, 2 слоя, подготовка Q3	Tikkurila G503 Farrow & Ball No. 89	32,56 7,21	Плинтус МДФ h=80 мм, аналог: МДФ под покраску 80×16	Tikkurila G503	15,9	Инженерная доска, 1167-4250, 2100×127 мм, на клею; тип 1, отм. ЧП +3,230	17,17	Н стен 2650 (до потолка); краска бренда веера G503 Tikkurila; матовая линейка класса 1 — по каталогу Tikkurila при закупке; краска бренда веера Little Greene класс по EN 13300 и блеск линейки — по ТУ Little Greene, в базе не сверены; плинтус в цвет: стены
7	Детская 12,30 м²	ГКЛ по каркасу П113, отм. +5,930; +6,030; окраска, Little Greene Absolute Matt, глубокоматовая, 2 слоя, подготовка Q3	Little Greene No. 222	12,30	Окраска, Tikkurila, полуматовая, 2 слоя, подготовка Q3 Акцент — стена А: окраска, Farrow & Ball, полуматовая, 2 слоя, подготовка Q3	Tikkurila G503 Farrow & Ball No. 66	24,01 10,10	Плинтус МДФ h=69 мм, SX165	Tikkurila G503	13,3	Инженерная доска, 1167-4250, 2100×127 мм, на клею; тип 1, отм. ЧП +3,230	12,30	Н стен 2700 (до потолка); краска бренда веера Little Greene; класс по EN 13300 и блеск линейки — по ТУ Little Greene, в базе не сверены; плинтус в цвет: стены
8	Гардеробная 3,82 м²	Потолок под покраску, отм. +6,130; окраска, Little Greene Absolute Matt, глубокоматовая, 2 слоя, подготовка Q3	Little Greene No. 222	3,82	Окраска, Little Greene Intelligent Matt, матовая, 2 слоя, подготовка Q3	Little Greene No. 222	22,06	Плинтус МДФ h=80 мм, аналог: МДФ под покраску 80×16	Little Greene No. 222	7,4	Инженерная доска, 1167-4250, 2100×127 мм, на клею; тип 1, отм. ЧП +3,230	3,82	Н стен 2900 (до потолка); краска бренда веера Little Greene; класс по EN 13300 и блеск линейки — по ТУ Little Greene, в базе не сверены; краска бренда веера Little Greene класс по EN 13300 и блеск линейки — по ТУ Little Greene, в базе не сверены; плинтус в цвет: стены
9	Кладовая 4,66 м²	Потолок под покраску, отм. +6,130; окраска, Tikkurila, глубокоматовая	NCS S 0300-N	4,66	Окраска, Tikkurila, матовая, подготовка Q3	NCS S 0502-Y	23,61	Плинтус МДФ h=69 мм, SX165	NCS S 0300-N	7,9	Инженерная доска, 1167-4250, 2100×127 мм, на клею; тип 1, отм. ЧП +3,230	4,66	Н стен 2900 (до потолка)

Примечания

1. Ведомость продолжена на листе 3 из 3; итоги, сводка площадей и примечания — на последнем листе ведомости.

Допущения и предложения на листе

Основа листа: взаимное расположение помещений, контур дома 9600 × 8000 и раскладка этажей подобраны проектировщиком под габариты помещений брифа; обмер и проект АР — задание (К-1); высота потолка 2900 мм — по брифу, не замерена; перекрытие 330 мм и отметка 2-го этажа +3,230 приняты; проект КР — задание (К-2); наружные стены 400 мм, перегородки 120 мм приняты (в брифе толщин нет) (К-1); разрешённая мощность 15 кВт принята по типовым ТУ для частного дома (К-4); подрайон климата не задан — принят не северный (жилые от 2,5 м) (К-7).

Знак «**» — предложение проектировщика, заказчиком не утверждено (согласовать с заказчиком): плинтус пом. 1–3, 5, 6, 8, 10, 11, фартук пом. 1 — артикул изделия не выбран: позиция описана характеристиками («аналог по характеристикам»), артикул выбирается при закупке; пол пом. 4, 13 — пирог пола: стяжка 33 мм и обмазочная гидроизоляция добавлены разработчиком проекта; артикул изделия не выбран: позиция описана характеристиками («аналог по характеристикам»), артикул выбирается при закупке.

См. лист открытых вопросов (лист 7, записи К-1, К-2, К-4; лист 8, запись К-7).

Изм.	Кол.уч	Лист	№ док.	Подп.	Дата
Разраб.		Кырлан А.С.			04.11.26
Пров.					
ГИП					
Н. контр.					
Утв.					

ГД-2026-012-АИ

Дом 120 м²

Общая площадь 147,36* м² · * размеры приняты, не замерены (реестр — л. 7–9, К-1)

Дизайн-проект интерьера

Стадия	Лист	Листов
РП	81	175

Ведомость отделки помещений. Лист 2 из 3

М б/м

Кырлан Александр Сергеевич

выпуск 04.11.2026 № 4dfa962484 · стр. 83 из 180

Ведомость отделки помещений. Лист 3 из 3

Потолки, стены, низ стен, полы · площади в м², длины в м · отметки в м

Ведомость отделки помещений (форма 1 прил. А ГОСТ 21.501-2018). Лист 3 из 3

№	Наименование помещения	Потолок			Стены и перегородки			Низ стен (плинтус)			Пол		Примечание
		Вид отделки	Код цвета	S, м²	Вид отделки	Код цвета	S, м²	Вид отделки	Код цвета	L, м	Вид отделки	S, м²	
10	Холл второго этажа 15,51 м²	ГКЛ по каркасу П113, отм. +6,030; окраска, Little Greene Absolute Matt, глубокоматовая, 2 слоя, подготовка Q3	Little Greene No. 222	15,51	Окраска, Tikkurila, матовая, 2 слоя, подготовка Q3	Tikkurila G503	33,04	Плинтус МДФ h=80 мм, аналог: МДФ под покраску 80×16	Tikkurila G503	11,1	Инженерная доска, 1167-4250, 2100×127 мм, на клею; тип 1, отм. ЧП +3,230	15,51	Н стен 2800 (до потолка); матовая моющаяся, класс 1 EN 13300 — осознанно вместо полуматовой; краска бренда веера G503 — Tikkurila матовая линейка класса 1 — по каталогу Tikkurila при закупке; краска бренда веера Little Greene; класс по EN 13300 и блеск линейки — по ТУ Little Greene, в базе не сверены; плинтус в цвет: стены
11	Коридор второго этажа 5,16 м²	ГКЛ по каркасу П113, отм. +5,980; окраска, Little Greene Absolute Matt, глубокоматовая, 2 слоя, подготовка Q3	Little Greene No. 222	5,16	Окраска, Tikkurila, матовая, 2 слоя, подготовка Q3	Tikkurila G503	17,94	Плинтус МДФ h=80 мм, аналог: МДФ под покраску 80×16	Tikkurila G503	5,7	Инженерная доска, 1167-4250, 2100×127 мм, на клею; тип 1, отм. ЧП +3,230	5,16	Н стен 2750 (до потолка); матовая моющаяся, класс 1 EN 13300 — осознанно вместо полуматовой; краска бренда веера G503 — Tikkurila матовая линейка класса 1 — по каталогу Tikkurila при закупке; краска бренда веера Little Greene; класс по EN 13300 и блеск линейки — по ТУ Little Greene, в базе не сверены; плинтус в цвет: стены
12	Детская вторая 9,23 м²	ГКЛ по каркасу П113, отм. +5,930; +6,030; окраска, Little Greene Absolute Matt, глубокоматовая, 2 слоя, подготовка Q3	Little Greene No. 222	9,23	Окраска, Tikkurila, полуматовая, 2 слоя, подготовка Q3 Акцент — стена А: окраска, Tikkurila, полуматовая, 2 слоя, подготовка Q3	Tikkurila G503 Tikkurila H440	22,32 6,80	Плинтус МДФ h=69 мм, SX165	Tikkurila G503	11,4	Инженерная доска, 1167-4250, 2100×127 мм, на клею; тип 1, отм. ЧП +3,230	9,23	Н стен 2700 (до потолка); краска бренда веера Little Greene; класс по EN 13300 и блеск линейки — по ТУ Little Greene, в базе не сверены; плинтус в цвет: стены
13	Санузел второго этажа 5,31 м²	ГКЛВ по каркасу П113, отм. +5,830; окраска, Little Greene Intelligent Bathroom, матовая, 2 слоя, подготовка Q3	Little Greene No. 222	5,31	Облицовка плиткой, A8UZ, 600×1200×9 мм, клей C2 TE S1, затирка CG2WA	Atlas Concorde A8UZ	19,06	нет			Аналог: керамогранит ректифицированный под травертин, матовый, 600×600×9 мм; тип 2, отм. ЧП +3,215	5,31	Н стен 2615 (до потолка); гидроизоляция обмазочная, 2 слоя, с заведением на стены 200 мм; над ванной — до 2000 и 300 мм за борт (по пирогу пола); тест проливом и акт скрытых работ; краска бренда веера Little Greene класс по EN 13300 и блеск линейки — по ТУ Little Greene, в базе не сверены
	Итого			**147,36**			**395,43**			**131,9**		**147,36**	

Допущения и предложения на листе. Знак «**» предложено (согласовать): плинтус пом. 1–3, 5, 6, 8, 10, 11, фартук пом. 1, пол пом. 4, 13. См. лист открытых вопросов (листы 7–9).

Примечания

1. Площади поверхностей — по чистым граням стен до отделки: стены = периметр × высоту от чистого пола помещения до низа потолка минус проёмы (облицовка плиткой — до верха облицовки); плинтус = периметр минус дверные проёмы; пол и потолок — по площади помещения. Количество плиток по раскладке. Площади помещений — с учётом всех частей помещения; откосы в площадь стен не входят.
2. Акцентные стены и фартук — отдельными строками, их площадь вычтена из основной отделки стен помещения; фартук — над нижними модулями кухни от столешницы до низа навесных шкафов, где шкафов нет — на 600 мм.
3. Плинтус — длина по периметру за вычетом дверных проёмов; примыкания к наличникам и встроенной мебели — по развёрткам.
4. Формат плитки — Ш×В×Т (ширина × высота в положении укладки × толщина), мм; на полу — вдоль стен А/В × вдоль стен Б/Г.
5. Коды цвета — по веерам производителей; колеровка каждой краски одной партией, проверка выкраса при свете D65 и при лампах проекта.
6. Уровни подготовки Q1–Q4 — система Knauf, не норма ГОСТ/СП; допуски поверхностей — по СП 71.13330.2017 (действующая редакция).
7. «аналог:» — изделие задано характеристиками, марку и артикул согласовать с заказчиком до закупки.
8. Сводка площадей по материалам, м²: потолок — Little Greene No. 222 Absolute Matt — 133,22; потолок — Little Greene No. 222 Intelligent Bathroom — 9,48; потолок — NCS S 0300-N — 4,66; стены — Tikkurila G503 — 266,47; стены — NCS S 3050-R80B — 10,31; стены — NCS S 5020-G90Y 10,47; стены — облицовка плиткой 600×1200×9 мм, Atlas Concorde A8UZ — 36,46; стены — Farrow & Ball No. 89 Modern Emulsion — 7,21; стены Farrow & Ball No. 66 — 10,10; стены — Little Greene No. 222 Intelligent Matt — 22,06; стены — NCS S 0502-Y — 23,61; стены — Tikkurila H440 6,80; фартук — облицовка керамогранитом 1200×600×9 мм — 1,94.

Изм.	Кол.уч	Лист	№ док.	Подп.	Дата
Разраб.		Кырлан А.С.			04.11.26
Пров.					
ГИП					
Н. контр.					
Утв.					

ГД-2026-012-АИ

Дом 120 м²

Общая площадь 147,36* м² · * размеры приняты, не замерены (реестр — л. 7–9, К-1)

Дизайн-проект интерьера

Стадия	Лист	Листов
РП	82	175

Ведомость отделки помещений. Лист 3 из 3

М б/м

Кырлан Александр Сергеевич

выпуск 04.11.2026 № 4dfa962484 · стр. 84 из 180

Колерная карта · 1-й этаж

Цвета и материалы по помещениям · палитра проекта · выкрасы на согласование

ПРЕДВАРИТЕЛЬНО · не для производства работ · открыто пунктов: 11 (реестр — л. 7–9)

Колерная карта по помещениям

Помещение	Поверхность	Образец	Поз.	Система и код цвета	Производитель, линейка / материал, артикул	Блеск	Класс истирания	LRV	Площадь
1. Гостиная-кухня 31,32 м²	стены		**К1**	Tikkurila G503	Tikkurila	матовая	1	89	40,0 м²
	акцент А		**К2**	NCS S 3050-R80B	Tikkurila	матовая	1	≈13	10,3 м²
	потолок		**К3**	Little Greene No. 222	Little Greene · Absolute Matt	глубокомат.	2	92	31,3 м²
	пол		**КМ1**	по образцу	Coswick · Вековые традиции · арт. 1167-4250				31,3 м²
	плинтус		**К4**	Tikkurila G503	МДФ · в цвет Tikkurila			89	21,7 м
	фартук		**КМ2**	по образцу	керамогранит · аналог по хар.				1,9 м²
2. Холл с лестницей 15,51 м²	стены		**К1**	Tikkurila G503	Tikkurila	матовая	1	89	40,0 м²
	потолок		**К3**	Little Greene No. 222	Little Greene · Absolute Matt	глубокомат.	2	92	15,5 м²
	пол		**КМ1**	по образцу	Coswick · Вековые традиции · арт. 1167-4250				15,5 м²
	плинтус		**К4**	Tikkurila G503	МДФ · в цвет Tikkurila			89	14,4 м
3. Кабинет 11 м²	стены		**К1**	Tikkurila G503	Tikkurila	матовая	1	89	23,0 м²
	акцент А		**К5**	NCS S 5020-G90Y	Tikkurila	матовая	1	≈20	10,5 м²
	потолок		**К3**	Little Greene No. 222	Little Greene · Absolute Matt	глубокомат.	2	92	11,0 м²
	пол		**КМ1**	по образцу	Coswick · Вековые традиции · арт. 1167-4250				11,0 м²
	плинтус		**К4**	Tikkurila G503	МДФ · в цвет Tikkurila			89	12,6 м
4. Санузел гостевой 4,17 м²	стены		**КМ3**	Marvel Travertine	Atlas Concorde · арт. A8UZ				18,5 м²
	потолок		**К6**	Little Greene No. 222	Little Greene · Intelligent Bathroom	матовая	1	92	4,2 м²
	пол		**КМ4**	по образцу	керамогранит · аналог по хар.				4,2 м²
5. Прихожая 12,2 м²	стены		**К1**	Tikkurila G503	Tikkurila	матовая	1	89	40,6 м²
	потолок		**К3**	Little Greene No. 222	Little Greene · Absolute Matt	глубокомат.	2	92	12,2 м²
	пол		**КМ5**	Marvel Travertine	Atlas Concorde · арт. A8UZ				12,2 м²
	плинтус		**К4**	Tikkurila G503	МДФ · в цвет Tikkurila			89	14,0 м

Перечень выкрасов на согласование

№	Код	Бренд / веер	Пом. / стена	Подложка	Формат	Статус
1	G503	Tikkurila	1, 2, 3, 5	ГКЛ с грунтом; МДФ под эмаль	600×1000; 300×600	к выполнению
2	S 3050-R80B	NCS Tikkurila	1 А	ГКЛ с грунтом	600×1000	к выполнению
3	No. 222	Little Greene	1, 2, 3, 4, 5	ГКЛ с грунтом	600×1000	к выполнению
4	S 5020-G90Y	NCS Tikkurila	3 А	ГКЛ с грунтом	600×1000	к выполнению

Схема квартиры: цвет стен и акценты (б/м)

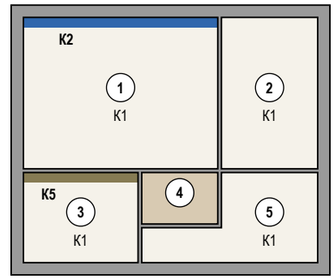


Схема палитры проекта

Стиль: Средиземноморский 60% + Скандинавский 40% · схема: комплементарная

основной	основной	второстепенный	второстепенный	второстепенный	акцентный	акцентный	акцентный
Tikkurila G503	**Little Greene No. 222**	**NCS S 1010-Y20R**	**Farrow & Ball No. 89**	**Farrow & Ball No. 292**	**NCS S 3050-R80B**	**Farrow & Ball No. 66**	**NCS S 5020-G90Y**
Calla LRV 89 стены 1,2,3,5; плинтус 1,2,3,5	Loft White LRV 92 потолок 1,2,3,4,5; текстиль/декор 1,3	Светлый песок / известняк LRV 75 текстиль/декор 1,3	Lulworth Blue — светлая морская лазурь LRV ≈45 в отделке не применён	Treron — серо-оливковая листва LRV 15 в отделке не применён	Эгейский синий LRV ≈13 акцент 1; текстиль/декор 1	India Yellow – охра / горчица итальянских фасадов LRV 36 в отделке не применён	Олива LRV ≈20 акцент 3; текстиль/декор 3

План 60/30/10

60%	30%	10%

Окраска, факт — по площади стен, акцентов, потолков

91%	9%

окрашено всего 238,5 м²; второстепенный тон несут мебель и текстиль

Текстиль и декор в цветах вне палитры проекта

Tikkurila X463 X463 Sandstone — песчаник — пом. 1 (T15, T16, T19), 3 (T9)

Условные обозначения

- **К1** Tikkurila G503 · Calla · краска · матовая · кл. 1
- **К2** NCS S 3050-R80B · Эгейский синий · Tikkurila · матовая · кл. 1
- **К3** Little Greene No. 222 · Loft White · Absolute Matt · глубокомат. · кл. 2
- **К4** Tikkurila G503 · Calla · МДФ
- **К5** NCS S 5020-G90Y · Олива · Tikkurila · матовая · кл. 1
- **К6** Little Greene No. 222 · Loft White · Intelligent Bathroom · матовая · кл. 1
- дерево (доска, паркет, ламинат) — рисунок досок
- керамогранит, плитка, камень — сетка швов по формату
- **КМ1** инженерная доска · 1167-4250
- **КМ2** аналог: керамогранит под травертин, матовый, 1200×600×9 мм
- **КМ3** плитка · A8UZ
- **КМ4** аналог: керамогранит ректифицированный под травертин, матовый, 600×600×9 мм
- **КМ5** керамогранит · A8UZ

К — краска, КМ — отделочный материал (тон КМ — по описанию, эталон — образец материала); кл. — класс истирания (1 — самый стойкий к мытью); LRV — светлота цвета: 0 — чёрный, 100 — белый; «≈» — ориентировочно

Примечания

1. Цвет на листе и на экране — ориентир. До покраски — выкрас на объекте: не меньше А3 (или лист ГКЛ), на грунте под эту краску, не на белой шпаклёвке, в 2 слоя; на обороте — код, бренд, веер, дата. Смотреть днём и вечером, рядом с образцами пола и плитки; к основному цвету стен — ещё 2 соседних оттенка. Красить только в цвет утверждённого выкраса.
2. Краску заказывать по коду из графы «Система и код цвета» у бренда этого кода, не «аналогом» другого; весь объём одного кода — одной партией, колеруемую краску — за один проход машины.
3. Площади — те же, что в ведомости отделки (лист 80); сколько краски заказать — в спецификации отделочных материалов (лист 86).

Допущения и предложения на листе

Основа листа: взаимное расположение помещений, контур дома 9600 × 8000 и раскладка этажей подобраны проектировщиком под габариты помещений брифа; обмер и проект АР — задание (К-1); высота потолка 2900 мм — по брифу, не замерена; перекрытие 330 мм и отметка 2-го этажа +3,230 приняты; проект КР — задание (К-2); наружные стены 400 мм, перегородки 120 мм приняты (в брифе толщин нет) (К-1); разрешённая мощность 15 кВт принята по типовым ТУ для частного дома (К-4); подрайон климата не задан — принят не северный (жилые от 2,5 м) (К-7).

Знак «**» — предложение проектировщика, заказчиком не утверждено (согласовать с заказчиком): плинтус пом. 1–3, 5, 6, 8, 10, 11, фартук пом. 1 — артикул изделия не выбран: позиция описана характеристиками («аналог по характеристикам»), артикул выбирается при закупке; пол пом. 4, 13 — пирог пола: стяжка 33 мм и обмазочная гидроизоляция добавлены разработчиком проекта; артикул изделия не выбран: позиция описана характеристиками («аналог по характеристикам»), артикул выбирается при закупке.

См. лист открытых вопросов (лист 7, записи К-1, К-2, К-4; лист 8, запись К-7).

Изм.	Кол.уч	Лист	№ док.	Подп.	Дата
Разраб.		Кырлан А.С.			04.11.26
Пров.					
ГИП					
Н. контр.					
Утв.					

ГД-2026-012-АИ

Дом 120 м²

Общая площадь 147,36* м² · * размеры приняты, не замерены (реестр — л. 7–9, К-1)

Дизайн-проект интерьера

Стадия	Лист	Листов
РП	83	175

Колерная карта · 1-й этаж

М б/м

Кырлан Александр Сергеевич

выпуск 04.11.2026 № 4dfa962484 · стр. 85 из 180

Колерная карта · 2-й этаж

Цвета и материалы по помещениям · палитра проекта · выкрасы на согласование

ПРЕДВАРИТЕЛЬНО · не для производства работ · открыто пунктов: 11 (реестр — л. 7–9)

Колерная карта по помещениям

Помещение	Поверхность	Образец	Поз.	Система и код цвета	Производитель, линейка / материал, артикул	Блеск	Класс истирания	LRV	Площадь
6. Спальня родителей 17,17 м²	стены		**K1**	Tikkurila G503	Tikkurila	матовая	1	89	32,6 м²
	акцент А		**K2**	Farrow & Ball No. 89	Farrow & Ball · Modern Emulsion	матовая	1	≈45	7,2 м²
	потолок		**K3**	Little Greene No. 222	Little Greene · Absolute Matt	глубокомат.	2	92	17,2 м²
	пол		**KM1**	по образцу	Coswick · Вековые традиции · арт. 1167-4250				17,2 м²
	плинтус		**K4**	Tikkurila G503	МДФ · в цвет Tikkurila			89	15,9 м
7. Детская 12,3 м²	стены		**K5**	Tikkurila G503	Tikkurila	полуматов.	1	89	24,0 м²
	акцент А		**K6**	Farrow & Ball No. 66	Farrow & Ball	полуматов.	1	36	10,1 м²
	потолок		**K3**	Little Greene No. 222	Little Greene · Absolute Matt	глубокомат.	2	92	12,3 м²
	пол		**KM1**	по образцу	Coswick · Вековые традиции · арт. 1167-4250				12,3 м²
	плинтус		**K7**	Tikkurila G503	Orac Decor · Contour (Luxxus)			89	13,3 м
8. Гардеробная 3,82 м²	стены		**K8**	Little Greene No. 222	Little Greene · Intelligent Matt	матовая	1	92	22,1 м²
	потолок		**K3**	Little Greene No. 222	Little Greene · Absolute Matt	глубокомат.	2	92	3,8 м²
	пол		**KM1**	по образцу	Coswick · Вековые традиции · арт. 1167-4250				3,8 м²
	плинтус		**K9**	Little Greene No. 222	МДФ · в цвет Little Greene			92	7,4 м
9. Кладовая 4,66 м²	стены		**K10**	NCS S 0502-Y	Tikkurila	матовая	2	86	23,6 м²
	потолок		**K11**	NCS S 0300-N	Tikkurila	глубокомат.	2	92	4,7 м²
	пол		**KM1**	по образцу	Coswick · Вековые традиции · арт. 1167-4250				4,7 м²
	плинтус		**K12**	NCS S 0300-N	Orac Decor · Contour (Luxxus)	полуматов.		92	7,9 м
10. Холл второго этажа 15,51 м²	стены		**K1**	Tikkurila G503	Tikkurila	матовая	1	89	36,8 м²
	потолок		**K3**	Little Greene No. 222	Little Greene · Absolute Matt	глубокомат.	2	92	15,5 м²
	пол		**KM1**	по образцу	Coswick · Вековые традиции · арт. 1167-4250				15,5 м²
	плинтус		**K4**	Tikkurila G503	МДФ · в цвет Tikkurila			89	12,9 м
11. Коридор второго этажа 5,16 м²	стены		**K1**	Tikkurila G503	Tikkurila	матовая	1	89	17,9 м²
	потолок		**K3**	Little Greene No. 222	Little Greene · Absolute Matt	глубокомат.	2	92	5,2 м²
	пол		**KM1**	по образцу	Coswick · Вековые традиции · арт. 1167-4250				5,2 м²
	плинтус		**K4**	Tikkurila G503	МДФ · в цвет Tikkurila			89	5,7 м
12. Детская вторая 9,23 м²	стены		**K5**	Tikkurila G503	Tikkurila	полуматов.	1	89	22,3 м²
	акцент А		**K13**	Tikkurila H440	Tikkurila	полуматов.	1	≈51	6,8 м²
	потолок		**K3**	Little Greene No. 222	Little Greene · Absolute Matt	глубокомат.	2	92	9,2 м²
	пол		**KM1**	по образцу	Coswick · Вековые традиции · арт. 1167-4250				9,2 м²
	плинтус		**K7**	Tikkurila G503	Orac Decor · Contour (Luxxus)			89	11,4 м
13. Санузел второго этажа 5,31 м²	стены		**KM2**	Marvel Travertine	Atlas Concorde · арт. A8UZ				20,7 м²
	потолок		**K14**	Little Greene No. 222	Little Greene · Intelligent Bathroom	матовая	1	92	5,3 м²
	пол		**KM3**	по образцу	керамогранит · аналог по хар.				5,3 м²

Схема палитры проекта


Стиль: Средиземноморский 60% + Скандинавский 40% · схема: комплементарная

основной **Tikkurila G503**	основной **Little Greene No. 222**	второстепенный **NCS S 1010-Y20R**	второстепенный **Farrow & Ball No. 89**	второстепенный **Farrow & Ball No. 292**	акцентный **NCS S 3050-R80B**	акцентный **Farrow & Ball No. 66**	акцентный **NCS S 5020-G90Y**
Calla LRV 89 стены 6,7,10,11,12; плинтус 6,7,10,11,12	Loft White LRV 92 потолок 6,7,8,10,11,12,13; стены 8; плинтус 8; текстиль/декор 6,7,12	Светлый песок / известняк LRV 75 текстиль/декор 6,7,12	Lulworth Blue — светлая морская лазурь LRV ≈45 акцент 6; текстиль/декор 6	Treron — серо-оливковая листва LRV 15 в отделке не применён	Эгейский синий LRV ≈13 в отделке не применён	India Yellow – охра / горчица итальянских фасадов LRV 36 акцент 7; текстиль/декор 7	Олива LRV ≈20 в отделке не применён

План 60/30/10



Окраска, факт — по площади стен, акцентов, потолков

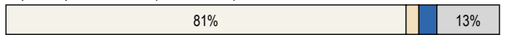

окрашено всего 276,6 м²; серым — цвета вне палитры; второстепенный тон несут мебель и текстиль

Текстиль и декор в цветах вне палитры проекта

- Tikkurila X395 X395 Playa — влажный пляжный песок — пом. 6 (T3)
- Tikkurila X463 X463 Sandstone — песчаник — пом. 7 (T22), 12 (T28)

Условные обозначения

- **K1** Tikkurila G503 · Calla · краска · матовая · кл. 1
- **K2** Farrow & Ball No. 89 · Lulworth Blue — светлая морская лазурь · Modern Emulsion · матовая · кл. 1
- **K3** Little Greene No. 222 · Loft White · Absolute Matt · глубокомат. · кл. 2
- **K4** Tikkurila G503 · Calla · МДФ
- **K5** Tikkurila G503 · Calla · краска · полуматов. · кл. 1
- **K6** Farrow & Ball No. 66 · India Yellow — охра / горчица итальянских фасадов · краска · полуматов. · кл. 1
- **K7** Tikkurila G503 · Calla · Contour (Luxxus)
- **K8** Little Greene No. 222 · Loft White · Intelligent Matt · матовая · кл. 1
- **K9** Little Greene No. 222 · Loft White · МДФ
- дерево (доска, паркет, ламинат) — рисунок досок
- керамогранит, плитка, камень — сетка швов по формату
- плашка не залита — цвет только по коду и вееру бренда
- **K10** NCS S 0502-Y · Tikkurila · матовая · кл. 2
- **K11** NCS S 0300-N · Tikkurila · глубокомат. · кл. 2
- **K12** NCS S 0300-N · Orac Decor Contour (Luxxus) · полуматов.
- **K13** Tikkurila H440 · H440 Wave — бирюзово-голубая вода · краска · полуматов. · кл. 1
- **K14** Little Greene No. 222 · Loft White · Intelligent Bathroom · матовая · кл. 1
- **KM1** инженерная доска · 1167-4250
- **KM2** плитка · A8UZ
- **KM3** аналог: керамогранит ректифицированный под травертин, матовый, 600×600×9 мм

К — краска, КМ — отделочный материал (тон КМ — по описанию, эталон — образец материала); кл. — класс истирания (1 — самый стойкий к мытью); LRV — светлота цвета: 0 — чёрный, 100 — белый; «≈» — ориентировочно

Перечень выкрасов на согласование

№	Код	Бренд / веер	Пом. / стена	Подложка	Формат	Статус
1	G503	Tikkurila	6, 7, 10, 11, 12	ГКЛ с грунтом; МДФ под эмаль	600×1000; 300×600	к выполнению

… ещё 6 выкрасов — в ведомости отделки

Примечания

1. Цвет на листе и на экране — ориентир. До покраски — выкрас на объекте: не меньше А3 (или лист ГКЛ), на грунте под эту краску, не на белой шпаклёвке, в 2 слоя; на обороте — код, бренд, веер, дата. Смотреть днём и вечером, рядом с образцами пола и плитки; к основному цвету стен — ещё 2 соседних оттенка. Красить только в цвет утверждённого выкраса.
2. Краску заказывать по коду из графы «Система и код цвета» у бренда этого кода, не «аналогом» другого; весь объём одного кода — одной партией, колеруемую краску — за один проход машины.
3. Площади — те же, что в ведомости отделки (лист 80); сколько краски заказать — в спецификации отделочных материалов (лист 86).

Допущения и предложения на листе. Основа листа: взаимное расположение помещений, контур дома 9600 × 8000 и раскладка этажей подобраны проектировщиком под габариты помещений брифа; обмер и проект АР — задание (К-1); высота потолка 2900 мм — по брифу, не замерена; перекрытие 330 мм и отметка 2-го этажа +3,230 приняты; проект КР — задание (К-2); наружные стены 400 мм, перегородки 120 мм приняты (в брифе толщин нет) (К-1); разрешённая мощность 15 кВт принята по типовым ТУ для частного дома (К-4); подрайон климата не задан — принят не северный (жилые от 2,5 м) (К-7). Знак «*» — принято, не замерено и не подтверждено (замерить на объекте): К-2: отметка чистого пола этажа «2-й этаж» +3,230 — отметка чистого пола 2-го этажа +3,230 принята: высота потолка 2900 по брифу + перекрытие с полом 330 (конструкция перекрытия не задана; проект КР — задание). Знак «**» — предложение проектировщика, заказчиком не утверждено (согласовать с заказчиком): плинтус пом. 1–3, 5, 6, 8, 10, 11, фартук пом. 1 — артикул изделия не выбран: позиция описана характеристиками («аналог по характеристикам»), артикул выбирается при закупке; пол пом. 4, 13 — пирог пола: стяжка 33 мм и обмазочная гидроизоляция добавлены разработчиком проекта; артикул изделия не выбран: позиция описана характеристиками («аналог по характеристикам»), артикул выбирается при закупке. См. лист открытых вопросов (лист 7, записи К-1, К-2, К-4; лист 8, запись К-7).

Изм.	Кол.уч	Лист	№ док.	Подп.	Дата
Разраб.		Кырлан А.С.			04.11.26
Пров.					
ГИП					
Н. контр.					
Утв.					

ГД-2026-012-АИ

Дом 120 м²

Общая площадь 147,36* м² · * размеры приняты, не замерены (реестр — л. 7–9, К-1)

Дизайн-проект интерьера

Стадия	Лист	Листов
РП	84	175

Колерная карта · 2-й этаж

М б/м

Кырлан Александр Сергеевич

выпуск 04.11.2026 № 4dfa962484 · стр. 86 из 180

Колерная карта

Цвета и материалы по помещениям · выкрасы на согласование · лист 2 из 2

Колерная карта по помещениям (продолжение)

Помещение	Поверхность	Образец	Поз.	Система и код цвета	Производитель, линейка / материал, артикул	Блеск	Класс истирания	LRV	Площадь
7. Детская 12,3 м²	стены		**K8**	Tikkurila G503	Tikkurila	полуматов.	1	89	24,0 м²
	акцент А		**K9**	Farrow & Ball No. 66	Farrow & Ball	полуматов.	1	36	10,1 м²
	потолок		**K3**	Little Greene No. 222	Little Greene · Absolute Matt	глубокомат.	2	92	12,3 м²
	пол		**KM1**	по образцу	Coswick · Вековые традиции · арт. 1167-4250				12,3 м²
	плинтус		**K10**	Tikkurila G503	Orac Decor · Contour (Luxxus)			89	13,3 м
8. Гардеробная 3,82 м²	стены		**K11**	Little Greene No. 222	Little Greene · Intelligent Matt	матовая	1	92	22,1 м²
	потолок		**K3**	Little Greene No. 222	Little Greene · Absolute Matt	глубокомат.	2	92	3,8 м²
	пол		**KM1**	по образцу	Coswick · Вековые традиции · арт. 1167-4250				3,8 м²
	плинтус		**K12**	Little Greene No. 222	МДФ · в цвет Little Greene			92	7,4 м
9. Кладовая 4,66 м²	стены		**K13**	NCS S 0502-Y	Tikkurila	матовая	2	86	23,6 м²
	потолок		**K14**	NCS S 0300-N	Tikkurila	глубокомат.	2	92	4,7 м²
	пол		**KM1**	по образцу	Coswick · Вековые традиции · арт. 1167-4250				4,7 м²
	плинтус		**K15**	NCS S 0300-N	Orac Decor · Contour (Luxxus)	полуматов.		92	7,9 м
10. Холл второго этажа 15,51 м²	стены		**K1**	Tikkurila G503	Tikkurila	матовая	1	89	33,0 м²
	потолок		**K3**	Little Greene No. 222	Little Greene · Absolute Matt	глубокомат.	2	92	15,5 м²
	пол		**KM1**	по образцу	Coswick · Вековые традиции · арт. 1167-4250				15,5 м²
	плинтус		**K4**	Tikkurila G503	МДФ · в цвет Tikkurila			89	11,1 м
11. Коридор второго этажа 5,16 м²	стены		**K1**	Tikkurila G503	Tikkurila	матовая	1	89	17,9 м²
	потолок		**K3**	Little Greene No. 222	Little Greene · Absolute Matt	глубокомат.	2	92	5,2 м²
	пол		**KM1**	по образцу	Coswick · Вековые традиции · арт. 1167-4250				5,2 м²
	плинтус		**K4**	Tikkurila G503	МДФ · в цвет Tikkurila			89	5,7 м
12. Детская вторая 9,23 м²	стены		**K8**	Tikkurila G503	Tikkurila	полуматов.	1	89	22,3 м²
	акцент А		**K16**	Tikkurila H440	Tikkurila	полуматов.	1	≈51	6,8 м²
	потолок		**K3**	Little Greene No. 222	Little Greene · Absolute Matt	глубокомат.	2	92	9,2 м²
	пол		**KM1**	по образцу	Coswick · Вековые традиции · арт. 1167-4250				9,2 м²
	плинтус		**K10**	Tikkurila G503	Orac Decor · Contour (Luxxus)			89	11,4 м
13. Санузел второго этажа 5,31 м²	стены		**KM3**	Marvel Travertine	Atlas Concorde · арт. A8UZ				19,1 м²
	потолок		**K6**	Little Greene No. 222	Little Greene · Intelligent Bathroom	матовая	1	92	5,3 м²
	пол		**KM4**	по образцу	керамогранит · аналог по хар.				5,3 м²

Условные обозначения

- **K1** Tikkurila G503 · Calla · краска · матовая · кл. 1
- **K2** NCS S 3050-R80B · Эгейский синий · Tikkurila · матовая · кл. 1
- **K3** Little Greene No. 222 · Loft White · Absolute Matt · глубокомат. · кл. 2
- **K4** Tikkurila G503 · Calla · МДФ
- **K5** NCS S 5020-G90Y · Олива · Tikkurila · матовая · кл. 1
- **K6** Little Greene No. 222 · Loft White · Intelligent Bathroom · матовая · кл. 1
- **K7** Farrow & Ball No. 89 · Lulworth Blue — светлая морская лазурь · Modern Emulsion · матовая · кл. 1
- **K8** Tikkurila G503 · Calla · краска · полуматов. · кл. 1
- **K9** Farrow & Ball No. 66 · India Yellow — охра / горчица итальянских фасадов · краска · полуматов. · кл. 1
- **K10** Tikkurila G503 · Calla · Contour (Luxxus)
- **K11** Little Greene No. 222 · Loft White · Intelligent Matt · матовая · кл. 1
- **K12** Little Greene No. 222 · Loft White · МДФ
- **K13** NCS S 0502-Y · Tikkurila · матовая · кл. 2
- **K14** NCS S 0300-N · Tikkurila · глубокомат. · кл. 2
- **K15** NCS S 0300-N · Orac Decor Contour (Luxxus) · полуматов.
- **K16** Tikkurila H440 · H440 Wave — бирюзово-голубая вода · краска · полуматов. · кл. 1
- **KM1** инженерная доска · 1167-4250
- **KM2** аналог: керамогранит под травертин, матовый, 1200×600×9 мм
- **KM3** плитка · A8UZ
- **KM4** аналог: керамогранит ректифицированный под травертин, матовый, 600×600×9 мм
- **KM5** керамогранит · A8UZ

дерево (доска, паркет, ламинат) — рисунок досок

керамогранит, плитка, камень — сетка швов по формату

плашка не залита — цвет только по коду и вееру бренда

К — краска, КМ — отделочный материал (тон КМ — по описанию, эталон — образец материала); кл. — класс истирания (1 — самый стойкий к мытью); LRV — светлота цвета: 0 — чёрный, 100 — белый; «≈» — ориентировочно

Перечень выкрасов на согласование

№	Код	Бренд / веер	Пом. / стена	Подложка	Формат	Статус
1	G503	Tikkurila	1, 2, 3, 5, 6, 7, 10, 11, 12	ГКЛ с грунтом; МДФ под эмаль	600×1000; 300×600	к выполнению
2	S 3050-R80B	NCS Tikkurila	1 А	ГКЛ с грунтом	600×1000	к выполнению
3	No. 222	Little Greene	1, 2, 3, 4, 5, 6, 7, 8, 10, 11, 12, 13	ГКЛ с грунтом; МДФ под эмаль	600×1000; 300×600	к выполнению
4	S 5020-G90Y	NCS Tikkurila	3 А	ГКЛ с грунтом	600×1000	к выполнению
5	No. 89	Farrow & Ball	6 А	ГКЛ с грунтом	600×1000	к выполнению
6	No. 66	Farrow & Ball	7 А	ГКЛ с грунтом	600×1000	к выполнению
7	S 0502-Y	NCS Tikkurila	9	ГКЛ с грунтом	600×1000	к выполнению
8	S 0300-N	NCS Tikkurila	9	ГКЛ с грунтом; МДФ под эмаль	600×1000; 300×600	к выполнению
9	H440	Tikkurila	12 А	ГКЛ с грунтом	600×1000	к выполнению

Примечания

1. Цвет на листе и на экране — ориентир. До покраски — выкрас на объекте: не меньше А3 (или лист ГКЛ), на грунте под эту краску, не на белой шпаклёвке, в 2 слоя; на обороте — код, бренд, веер, дата. Смотреть днём и вечером, рядом с образцами пола и плитки; к основному цвету стен — ещё 2 соседних оттенка. Красить только в цвет утверждённого выкраса.
2. Краску заказывать по коду из графы «Система и код цвета» у бренда этого кода, не «аналогом» другого; весь объём одного кода — одной партией, колеруемую краску — за один проход машины.
3. Площади — те же, что в ведомости отделки (лист 80); сколько краски заказать — в спецификации отделочных материалов (лист 86).
4. Колерная карта на 2 листах: обозначения — на каждом, схема и палитра — на первом, выкрасы — на последнем.

Допущения и предложения на листе. Основа листа: взаимное расположение помещений, контур дома 9600 × 8000 и раскладка этажей подобраны проектировщиком под габариты помещений брифа; обмер и проект АР — задание (К-1); высота потолка 2900 мм — по брифу, не замерена; перекрытие 330 мм и отметка 2-го этажа +3,230 приняты; проект КР — задание (К-2); наружные стены 400 мм, перегородки 120 мм приняты (в брифе толщин нет) (К-1); разрешённая мощность 15 кВт принята по типовым ТУ для частного дома (К-4); подрайон климата не задан — принят не северный (жилые от 2,5 м) (К-7). Знак «**» — предложение проектировщика, заказчиком не утверждено (согласовать с заказчиком): плинтус пом. 1–3, 5, 6, 8, 10, 11, фартук пом. 1 — артикул изделия не выбран: позиция описана характеристиками («аналог по характеристикам»), артикул выбирается при закупке; пол пом. 4, 13 — пирог пола: стяжка 33 мм и обмазочная гидроизоляция добавлены разработчиком проекта; артикул изделия не выбран: позиция описана характеристиками («аналог по характеристикам»), артикул выбирается при закупке. См. лист открытых вопросов (лист 7, записи К-1, К-2, К-4; лист 8, запись К-7).

Изм.	Кол.уч	Лист	№ док.	Подп.	Дата
Разраб.		Кырлан А.С.			04.11.26
Пров.					
ГИП					
Н. контр.					
Утв.					

ГД-2026-012-АИ

Дом 120 м²

Общая площадь 147,36* м² · * размеры приняты, не замерены (реестр — л. 7–9, К-1)

Дизайн-проект интерьера

Стадия	Лист	Листов
РП	85	175

Колерная карта

М б/м

Кырлан Александр Сергеевич

выпуск 04.11.2026 № 4dfa962484 · стр. 87 из 180

Спецификация отделочных материалов

Форма 1 по ГОСТ 21.110-2013 · количества — из геометрии проекта, с запасом · часть 1 из 2

ПРЕДВАРИТЕЛЬНО · не для производства работ · открыто пунктов: 11 (реестр — л. 7–9)

Поз.	Наименование и техническая характеристика	Тип, марка, обозначение документа	Код продукции	Поставщик	Ед. изм.	Кол.	Масса 1 ед., кг	Примечание
	Лакокрасочные материалы							
1	Краска интерьерная водно-дисперсионная акриловая для стен, матовая, класс мокрого истирания 1 по EN 13300, база A; цвет по вееру Tikkurila G503 «Calla», колеровка машинная	Tikkurila		Tikkurila	л	59,4		поз. К1 колерной карты; пом. 1, 2, 3, 5, 6, 10, 11; S = 220,1 м² × 2 сл. × 0,12 л/м² = 52,8 л, +10 % и 0,5 л на подкраску → ≥ 58,6 л; тара 6 × 9 л + 2 × 2,7 л
2	Краска интерьерная водно-дисперсионная акриловая для акцентных стен, матовая, класс мокрого истирания 1 по EN 13300, база C; цвет NCS S 3050-R80B «Эгейский синий», колеровка машинная	Tikkurila		Tikkurila	л	3,6		поз. К2 колерной карты; пом. 1; S = 10,3 м² × 2 сл. × 0,12 л/м² = 2,5 л, +10 % и 0,5 л на подкраску → ≥ 3,2 л; тара 1 × 2,7 л + 1 × 0,9 л
3	Краска интерьерная водно-дисперсионная акриловая для потолков, глубокоматовая, класс мокрого истирания 2 по EN 13300, база A; цвет по вееру Little Greene No. 222 «Loft White», колеровка машинная	Little Greene Absolute Matt		Little Greene	л	35,7		поз. К3 колерной карты; пом. 1, 2, 3, 5, 6, 7, 8, 10, 11, 12; S = 133,2 м² × 2 сл. × 0,12 л/м² = 32,0 л, +10 % и 0,5 л на подкраску → ≥ 35,7 л; тара — кратно фасовке продукта
4	Краска интерьерная водно-дисперсионная акриловая для акцентных стен, матовая, класс мокрого истирания 1 по EN 13300, база C; цвет NCS S 5020-G90Y «Олива», колеровка машинная	Tikkurila		Tikkurila	л	3,6		поз. К5 колерной карты; пом. 3; S = 10,5 м² × 2 сл. × 0,12 л/м² = 2,5 л, +10 % и 0,5 л на подкраску → ≥ 3,3 л; тара 1 × 2,7 л + 1 × 0,9 л
5	Краска интерьерная водно-дисперсионная акриловая для потолков, матовая, класс мокрого истирания 1 по EN 13300, база A; цвет по вееру Little Greene No. 222 «Loft White», колеровка машинная	Little Greene Intelligent Bathroom		Little Greene	л	3,1		поз. К6 колерной карты; пом. 4, 13; S = 9,5 м² × 2 сл. × 0,12 л/м² = 2,3 л, +10 % и 0,5 л на подкраску → ≥ 3,0 л; тара — кратно фасовке продукта
6	Краска интерьерная водно-дисперсионная акриловая для акцентных стен, матовая, класс мокрого истирания 1 по EN 13300, база C; цвет по вееру Farrow & Ball No. 89 «Lulworth Blue — светлая морская лазурь», колеровка машинная	Farrow & Ball Modern Emulsion		Farrow & Ball	л	2,5		поз. К7 колерной карты; пом. 6; S = 7,2 м² × 2 сл. × 0,12 л/м² = 1,7 л, +10 % и 0,5 л на подкраску → ≥ 2,4 л; тара 1 × 2,5 л
7	Краска интерьерная водно-дисперсионная акриловая для стен, полуматовая, класс мокрого истирания 1 по EN 13300, база A; цвет по вееру Tikkurila G503 «Calla», колеровка машинная	Tikkurila		Tikkurila	л	13,5		поз. К8 колерной карты; пом. 7, 12; S = 46,3 м² × 2 сл. × 0,12 л/м² = 11,1 л, +10 % и 0,5 л на подкраску → ≥ 12,7 л; тара 1 × 9 л + 1 × 2,7 л + 2 × 0,9 л
8	Краска интерьерная водно-дисперсионная акриловая для акцентных стен, полуматовая, класс мокрого истирания 1 по EN 13300, база C; цвет по вееру Farrow & Ball No. 66 «India Yellow — охра / горчица итальянских фасадов», колеровка машинная	Farrow & Ball		Farrow & Ball	л	5		поз. К9 колерной карты; пом. 7; S = 10,1 м² × 2 сл. × 0,12 л/м² = 2,4 л, +10 % и 0,5 л на подкраску → ≥ 3,2 л; тара 1 × 5 л
9	Краска интерьерная водно-дисперсионная акриловая для стен, матовая, класс мокрого истирания 1 по EN 13300, база A; цвет по вееру Little Greene No. 222 «Loft White», колеровка машинная	Little Greene Intelligent Matt		Little Greene	л	6,4		поз. К11 колерной карты; пом. 8; S = 22,1 м² × 2 сл. × 0,12 л/м² = 5,3 л, +10 % и 0,5 л на подкраску → ≥ 6,3 л; тара — кратно фасовке продукта
10	Краска интерьерная водно-дисперсионная акриловая для стен, матовая, класс мокрого истирания 2 по EN 13300, база A; цвет NCS S 0502-Y, колеровка машинная	Tikkurila		Tikkurila	л	7,2		поз. К13 колерной карты; пом. 9; S = 23,6 м² × 2 сл. × 0,12 л/м² = 5,7 л, +10 % и 0,5 л на подкраску → ≥ 6,7 л; тара 2 × 2,7 л + 2 × 0,9 л
11	Краска интерьерная водно-дисперсионная для потолков, глубокоматовая, класс мокрого истирания 2 по EN 13300, база A; цвет NCS S 0300-N, колеровка машинная	Tikkurila		Tikkurila	л	1,8		поз. К14 колерной карты; пом. 9; S = 4,7 м² × 2 сл. × 0,12 л/м² = 1,1 л, +10 % и 0,5 л на подкраску → ≥ 1,7 л; тара 2 × 0,9 л
12	Краска интерьерная водно-дисперсионная акриловая для акцентных стен, полуматовая, класс мокрого истирания 1 по EN 13300, база C; цвет по вееру Tikkurila H440 «H440 Wave — бирюзово-голубая вода», колеровка машинная	Tikkurila		Tikkurila	л	2,7		поз. К16 колерной карты; пом. 12; S = 6,8 м² × 2 сл. × 0,12 л/м² = 1,6 л, +10 % и 0,5 л на подкраску → ≥ 2,3 л; тара 1 × 2,7 л
13	Краска для МДФ и дерева в цвет Tikkurila G503 «Calla» — окраска плинтуса; блеск не ниже блеска стен	марка не задана			л	2,9		поз. К4, К10; пом. 1, 2, 3, 5, 6, 7, 10, 11, 12; L = 116,5 м, S = 10,9 м² × 2 сл. × 0,12 л/м² + 10 %; продукт подобрать в веере Tikkurila
14	Краска для МДФ и дерева в цвет Little Greene No. 222 «Loft White» — окраска плинтуса; блеск не ниже блеска стен	марка не задана			л	0,5		поз. К12; пом. 8; L = 7,4 м, S = 0,7 м² × 2 сл. × 0,12 л/м² + 10 %; продукт подобрать в веере Little Greene
15	Акрил, полуматовая в цвет NCS S 0300-N — окраска плинтуса	аналог по характеристикам			л	0,5		поз. К15; пом. 9; L = 7,9 м, S = 0,7 м² × 2 сл. × 0,12 л/м² + 10 %; продукт подобрать в веере NCS
16	Грунтовка акриловая под окраску стен и потолков — из системы производителя краски	по системе краски			м²	505		площадь окраски стен, акцентов и потолков; 1 слой перед окраской; расход — по ТУ грунтовки

Допущения и предложения на листе

Основа листа: взаимное расположение помещений, контур дома 9600 × 8000 и раскладка этажей подобраны проектировщиком под габариты помещений брифа; обмер и проект АР — задание (К-1); высота потолка 2900 мм — по брифу, не замерена; перекрытие 330 мм и отметка 2-го этажа +3,230 приняты; проект КР — задание (К-2); наружные стены 400 мм, перегородки 120 мм приняты (в брифе толщин нет) (К-1); разрешённая мощность 15 кВт принята по типовым ТУ для частного дома (К-4); подрайон климата не задан — принят не северный (жилые от 2,5 м) (К-7).

Знак «**» — предложение проектировщика, заказчиком не утверждено (согласовать с заказчиком): плинтус пом. 1–3, 5, 6, 8, 10, 11, фартук пом. 1 — артикул изделия не выбран: позиция описана характеристиками («аналог по характеристикам»), артикул выбирается при закупке; пол пом. 4, 13 — пирог пола: стяжка 33 мм и обмазочная гидроизоляция добавлены разработчиком проекта; артикул изделия не выбран: позиция описана характеристиками («аналог по характеристикам»), артикул выбирается при закупке.

См. лист открытых вопросов (лист 7, записи К-1, К-2, К-4; лист 8, запись К-7).

Изм.	Кол.уч	Лист	№ док.	Подп.	Дата
Разраб.		Кырлан А.С.			04.11.26
Пров.					
ГИП					
Н. контр.					
Утв.					

ГД-2026-012-АИ

Дом 120 м²

Общая площадь 147,36* м² · * размеры приняты, не замерены (реестр — л. 7–9, К-1)

Дизайн-проект интерьера

Стадия	Лист	Листов
РП	86	175

Спецификация отделочных материалов

М б/м

Кырлан Александр Сергеевич

Спецификация отделочных материалов

Форма 1 по ГОСТ 21.110-2013 · количества — из геометрии проекта, с запасом · часть 2 из 2

ПРЕДВАРИТЕЛЬНО · не для производства работ · открыто пунктов: 11 (реестр — л. 7–9)

Поз.	Наименование и техническая характеристика	Тип, марка, обозначение документа	Код продукции	Поставщик	Ед. изм.	Кол.	Масса 1 ед., кг	Примечание
	Плитка и керамогранит							
17	Керамогранит под травертин, 600×600×9 мм, ректификат, водопоглощение 0,1 % (BIa), противоскольжение R10, PEI IV	аналог по характеристикам			м²	14,04		шов 2 мм; Санузел гостевой, пол; Санузел второго этажа, пол; по раскладке 35 шт (S = 9,48 м²), с запасом 39 шт
18	A8UZ, 600×1200×9 мм, ректификат, водопоглощение 0,1 % (BIa), противоскольжение R10, PEI IV	A8UZ		Atlas Concorde	м²	83,52		шов 2 мм; Санузел гостевой, стены А–Г; Санузел гостевой, короб инсталляции; Санузел второго этажа, стены А–Г; Санузел второго этажа, короб инсталляции; Прихожая, пол; по раскладке 103 шт (S = 50,21 м²), с запасом 116 шт
19	Керамогранит под травертин, матовый, 1200×600×9 мм, ректификат, водопоглощение 0,1 % (BIa)	аналог по характеристикам			м²	6,48		шов 2 мм; Гостиная-кухня, фартук (ст. А); Гостиная-кухня, фартук (ст. Б); по раскладке 7 шт (S = 1,94 м²), с запасом 9 шт
	Напольные покрытия							
20	1167-4250, рабочий слой 4 мм, эмиссия E1, укладка на клей	1167-4250		Coswick	м²	129,5		пом. 1, 2, 3, 6, 7, 8, 10, 11, 12; S = 121,02 м² + 7 % (прямая укладка); к заказу — кратно упаковке
21	1167-4250, класс 33, рабочий слой 4 мм, эмиссия E1, укладка на клей	1167-4250		Coswick	м²	5		пом. 9; S = 4,66 м² + 7 % (прямая укладка); к заказу — кратно упаковке
22	Клей для паркета и инженерной доски, эластичный (СМП / полиуретановый)	по рекомендации производителя доски			м²	126		площадь приклейки; расход и шпатель — по ТУ клея
	Погонажные изделия							
23	Плинтус МДФ под покраску 80×16, крепление к стене, окраска в цвет Tikkurila G503	аналог по характеристикам			м	102		пом. 1, 2, 3, 5, 6, 10, 11; L = 91,9 м (периметр без дверных проёмов) + 10 % на подрезку; в штуках — по длине планки
24	SX165, h = 69 мм, крепление к стене, окраска в цвет Tikkurila G503	SX165		Orac Decor	м	28		пом. 7, 12; L = 24,6 м (периметр без дверных проёмов) + 10 % на подрезку; в штуках — по длине планки
25	Плинтус МДФ под покраску 80×16, крепление к стене, окраска в цвет Little Greene No. 222	аналог по характеристикам			м	9		пом. 8; L = 7,4 м (периметр без дверных проёмов) + 10 % на подрезку; в штуках — по длине планки
26	SX165, h = 69 мм, крепление к стене, окраска в цвет NCS S 0300-N	SX165		Orac Decor	м	9		пом. 9; L = 7,9 м (периметр без дверных проёмов) + 10 % на подрезку; в штуках — по длине планки
	Смеси и материалы для облицовки							
27	Затирка для швов плитки, класс CG2WA по EN 13888	Mapei Ultracolor Plus 132		Mapei	кг	5,2		по раскладке (a+b)/(a·b) × шов × t × 1,6 + 10 %; в т. ч. 1,1 кг — позиции раскладки без марки
28	Клей плиточный C2 TE S1 по EN 12004, слой 5 мм	Ceresit CM 17		Ceresit	кг	516		21 меш. по 25 кг; 1,5 кг/м² на 1 мм слоя + 10 %; в т. ч. 115 кг — позиции раскладки без марки
29	Гидроизоляция обмазочная мокрых зон: пол, стены по периметру, зоны замачивания; 2 слоя с армирующей лентой в углах	аналог по характеристикам			м²	19,6		площадь по листу раскладки плитки + 10 %; расход смеси — по ТУ
30	Лента демпферная по периметру пола из плитки	аналог по характеристикам			м	33,3		периметр без дверных проёмов + 10 %

Примечания

1. Количества — из геометрии проекта: площади поверхностей по чистым граням стен до отделки (те же, что в ведомости отделки и колерной карте), плитка, клей и затирка — по раскладке плиточника; в графе «Кол.» — к заказу, с запасом.
2. Краска: расход 0,12 л/м² на слой в 2 слоя, если по ТУ не задан иной; запас 10 % и 0,5 л на подкраску каждого кода. Один код — одна партия, колеровка машинная в колеровочном центре бренда; в заказ — только после утверждения выкраса (колерная карта). Фасовка — по каталогу бренда на дату выпуска; к заказу — не меньше расчётного объёма.
3. «Аналог по характеристикам» — допускается изделие другого производителя с характеристиками не ниже указанных, по согласованию с автором проекта.
4. Графы «Код продукции» и «Масса 1 ед.» не заполнены: коды по классификатору продукции не присвоены, масса единицы до 25 кг (ГОСТ 21.110-2013).
5. Грунтовка и клей для доски указаны площадью обработки; объём — по ТУ выбранного продукта.

Допущения и предложения на листе

Основа листа: взаимное расположение помещений, контур дома 9600 × 8000 и раскладка этажей подобраны проектировщиком под габариты помещений брифа; обмер и проект АР — задание (К-1); высота потолка 2900 мм — по брифу, не замерена; перекрытие 330 мм и отметка 2-го этажа +3,230 приняты; проект КР — задание (К-2); наружные стены 400 мм, перегородки 120 мм приняты (в брифе толщин нет) (К-1); разрешённая мощность 15 кВт принята по типовым ТУ для частного дома (К-4); подрайон климата не задан — принят не северный (жилые от 2,5 м) (К-7).

Знак «**» — предложение проектировщика, заказчиком не утверждено (согласовать с заказчиком): плинтус пом. 1–3, 5, 6, 8, 10, 11, фартук пом. 1 — артикул изделия не выбран: позиция описана характеристиками («аналог по характеристикам»), артикул выбирается при закупке; пол пом. 4, 13 — пирог пола: стяжка 33 мм и обмазочная гидроизоляция добавлены разработчиком проекта; артикул изделия не выбран: позиция описана характеристиками («аналог по характеристикам»), артикул выбирается при закупке.

См. лист открытых вопросов (лист 7, записи К-1, К-2, К-4; лист 8, запись К-7).

Изм.	Кол.уч	Лист	№ док.	Подп.	Дата
Разраб.		Кырлан А.С.			04.11.26
Пров.					
ГИП					
Н. контр.					
Утв.					

ГД-2026-012-АИ

Дом 120 м²

Общая площадь 147,36* м² · * размеры приняты, не замерены (реестр — л. 7–9, К-1)

Дизайн-проект интерьера

Стадия	Лист	Листов
РП	87	175

Спецификация отделочных материалов

М б/м

Кырлан Александр Сергеевич

выпуск 04.11.2026 № 4dfa962484 · стр. 89 из 180

Концепция декора и визуализации

Средиземноморский · визуализации, палитра, материалы, ключевые предметы

ПРЕДВАРИТЕЛЬНО · не для производства работ · открыто пунктов: 11 (реестр — л. 7–9)



Визуализация 1. Вид сверху (3D): планировка с мебелью, текстилем и декором

Расстановка — по плану мебели (лист 27); шторы, ковры, картины и растения — по плану текстиля и декора (лист 89).



Визуализация 15. Гостиная-кухня (пом. 1)

шторы Т13, Т14, Т15 · ковёр Т16 · картина ДК6 · растение ДК7, ДК40 · подушки, пледы Т17, Т18, Т19



Визуализация 4. Спальня родителей (пом. 6)

шторы Т1, Т2 · ковёр Т3 · картина ДК1 · растение ДК44 · подушки, пледы Т4, Т5, Т6



Визуализация 11. Детская (пом. 7)

шторы Т20, Т21 · ковёр Т22 · картина ДК2 · зеркало ДК4 · подушки, пледы Т23, Т24, Т25



Визуализация 13. Детская вторая (пом. 12)

шторы Т26, Т27 · ковёр Т28 · картина ДК10 · зеркало ДК11 · подушки, пледы Т29, Т30, Т31

Материалы и фактуры



Дуб натуральный

пол: пом. 1, 2, 3, 6, 7, 8, 9, 10, 11, 12; рамы ДК1, ДК2, ДК3,



Травертин (керамогранит)

пол и стены санузлов, фартук: пом. 1, 4, 13




Букле

подушки: Т10, Т17, Т23, Т29



Лён

портьеры, римская штора, подушки: Т1, Т4, Т7, Т13, Т15, Т20, Т26

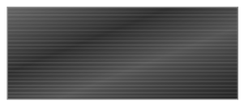

Чёрный матовый металл

рамы ДК4, ДК5, ДК11 — чёрный

Ключевые предметы

— Диван Гс2 2400×950 — гостиная-кухня; подушки и плед Т17, Т18, Т19

— Кровати Дт1, Дт6, М1 — над изголовьем картины ДК1, ДК2, ДК10; текстиль Т4, Т5, Т6, Т23, Т24, Т25, Т29, Т30, Т31

— Ковры Т3, Т9, Т16, Т22, Т28 — шерсть, на противоскользящей подложке

— Картины ДК1, ДК2, ДК3, ДК6, ДК10 — центр на высоте 875–1650 мм

— Зеркала в рост ДК4, ДК5, ДК11; над умывальниками ДК9, ДК12

— Шторы-волна Т1, Т7, Т13, Т20, Т26 (NCS S 1010-Y20R), тюль Т2, Т8, Т14, Т21, Т27 (Little Greene No. 222) — в нишах потолка

— Растение ДК7, ваза ДК8, растение ДК40, растение ДК41, растение ДК43, растение ДК44, растение ДК45, растение ДК46

Настроение

Средиземноморский 60 % + скандинавский 40 %: дом у соснового бора, светлый и солнечный. Стены — кремовый белый Calla G503, потолки — Loft White No. 222; второй план — светлый песок S 1010-Y20R, морская лазурь Lulworth Blue No. 89, серо-оливковая листва Treron No. 292; акценты — эгейский синий S 3050-R80B, охра India Yellow No. 66, олива S 5020-G90Y. По брифу: дерево — дуб табак (мебель, лестница), фурнитура и светильники — латунь, рамы и металл — тёплый графит; свет тёплый 2700–3000 K, фасады матовые. Настроение стиля: солнце и воздух, морская свежесть, неторопливость, тёплая простота, жизнь на террасе. Свет тёплый, 2700–3000 K.

Примечания

1. Визуализации — образ интерьера. Изделия, размеры, высоты подвеса и привязки — по чертежам (план текстиля и декора — лист 89; шторы и карнизы — лист 91; ведомость текстиля — лист 92; ведомость декора и развеска — лист 94); при расхождении действуют чертежи и ведомости.
2. Коды цвета — ориентир подбора по веерам производителей; ткань утверждается по образцу при дневном свете и при свете проекта 2700–3000 K.
3. Мелкий стайлинг на визуализациях (книги, посуда, свечи) в ведомости не входит и поставляется заказчиком по желанию.

Палитра 60/30/10 и цвета текстиля



- Tikkurila G503 (Calla), LRV 89 — 60 % база
- Little Greene No. 222 (Loft White), LRV 92 — 60 % база — Т2, Т8, Т14, Т21, Т27
- NCS S 1010-Y20R (Светлый песок / известняк), LRV 75 — 30 % второй цвет — Т1, Т4, Т7, Т10, Т13, Т17, Т20, Т23, Т26, Т29
- Farrow & Ball No. 89 (Lulworth Blue — светлая морская лазурь), LRV 45 — 30 % второй цвет — Т5, Т6
- Farrow & Ball No. 292 (Treron — серо-оливковая листва), LRV 15 — 30 % второй цвет
- NCS S 3050-R80B (Эгейский синий), LRV 13 — 10 % акцент — Т18
- Farrow & Ball No. 66 (India Yellow — охра / горчица итальянских фасадов), LRV 36 — 10 % акцент — Т24, Т25
- NCS S 5020-G90Y (Олива), LRV 20 — 10 % акцент — Т11, Т12
- Tikkurila X463, LRV 51 — текстиль — Т9, Т15, Т16, Т19, Т22, Т28
- Tikkurila X395, LRV 53 — текстиль — Т3

Допущения и предложения на листе. Основа листа: взаимное расположение помещений, контур дома 9600 × 8000 и раскладка этажей подобраны проектировщиком под габариты помещений брифа; обмер и проект АР — задание (К-1); высота потолка 2900 мм — по брифу, не замерена; перекрытие 330 мм и отметка 2-го этажа +3,230 приняты; проект КР — задание (К-2); наружные стены 400 мм, перегородки 120 мм приняты (в брифе толщин нет) (К-1); разрешённая мощность 15 кВт принята по типовым ТУ для частного дома (К-4); подрайон климата не задан — принят не северный (жилые от 2,5 м) (К-7). См. лист открытых вопросов (лист 7, записи К-1, К-2, К-4; лист 8, запись К-7).

Изм.	Кол.уч	Лист	№ док.	Подп.	Дата
Разраб.		Кырлан А.С.			04.11.26
Пров.					
ГИП					
Н. контр.					
Утв.					

ГД-2026-012-АИ

Дом 120 м²

Общая площадь 147,36* м² · * размеры приняты, не замерены (реестр — л. 7–9, К-1)

Дизайн-проект интерьера

Стадия	Лист	Листов
РП	88	175

Концепция декора и визуализации

М б/м


Кырлан Александр Сергеевич

выпуск 04.11.2026 № 4dfa962484 · стр. 90 из 180

План текстиля и декора · 1-й этаж

Шторы и карнизы, ковры, картины и зеркала, растения · размеры в мм от чистовых стен и чистого пола · марки — по ведомостям

ПРЕДВАРИТЕЛЬНО · не для производства работ · открыто пунктов: 11 (реестр — л. 7–9)

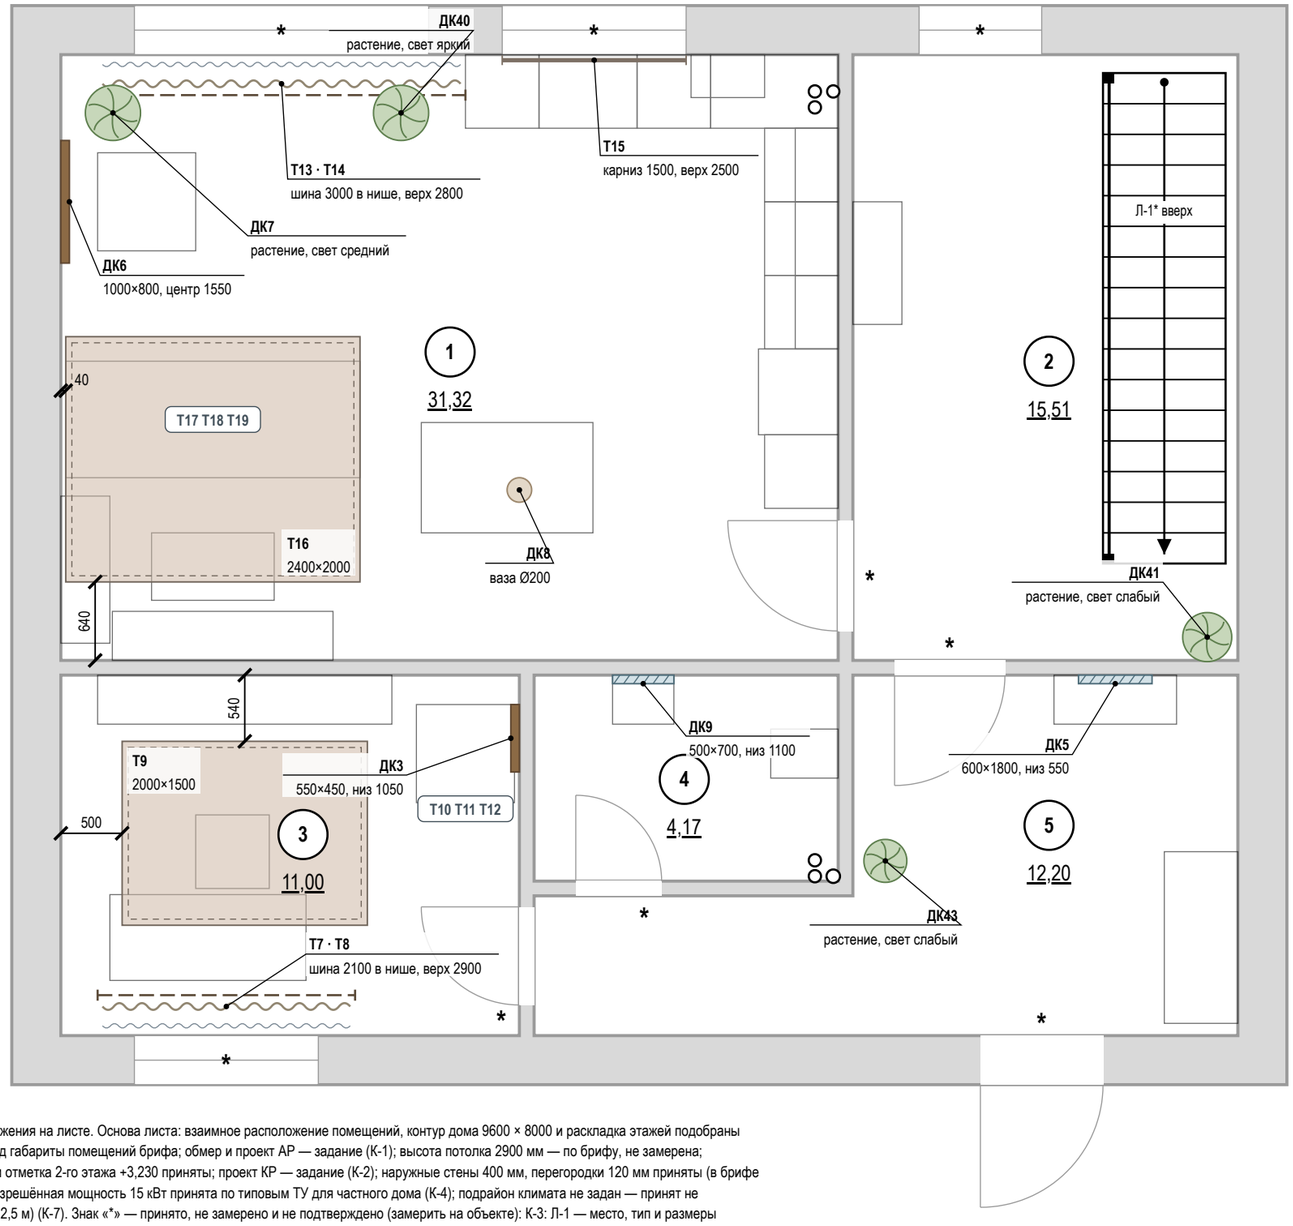

Допущения и предложения на листе. Основа листа: взаимное расположение помещений, контур дома 9600 × 8000 и раскладка этажей подобраны проектировщиком под габариты помещений брифа; обмер и проект АР — задание (К-1); высота потолка 2900 мм — по брифу, не замерена; перекрытие 330 мм и отметка 2-го этажа +3,230 приняты; проект КР — задание (К-2); наружные стены 400 мм, перегородки 120 мм приняты (в брифе толщин нет) (К-1); разрешённая мощность 15 кВт принята по типовым ТУ для частного дома (К-4); подрайон климата не задан — принят не северный (жилые от 2,5 м) (К-7). Знак «*» — принято, не замерено и не подтверждено (замерить на объекте): К-3: Л-1 — место, тип и размеры лестницы брифом не заданы (только «лестница из холла 1-го этажа»): одномаршевая 17 × 190 × 250 вдоль стены Б холла — предложение проектировщика; конструкция и расчёт — проект КР; К-5: Ст К1-1, Ст В1-1, Ст Т3-1, Ст К1-2 (кухня), Ст В1-2, Ст Т3-2 — положение стояка принято проектировщиком (проект ВК дома не передан), не замерено. См. лист открытых вопросов (лист 7, записи К-1–К-5; лист 8, запись К-7).

Примечания

1. Размеры — в мм. Отступы ковров — от чистовых стен; высоты картин и зеркал — от чистого пола до центра или низа рамы.
2. Шторы — на шинах в нишах потолка (ниша — план потолков, лист 66); закладная под шину — до обшивки ГКЛ. Схемы окон, длины полотен и сборка — лист 91.
3. Картины и зеркала массой более 5 кг — на анкеры по основанию, нагрузка крепежа не меньше двойной массы изделия; на ГКЛ — только по закладной. Декор не перекрывает розетки и выключатели.
4. Ковры на гладком полу — на противоскользящей подложке.
5. Мебель — по плану расстановки мебели (лист 27); ведомость текстиля — лист 92, ведомость декора и схемы развески — лист 94.
6. Знак «*» у проёма — допущение: положение проёма не замерено (окно пом. 1, стена А (2 шт.); дверь пом. 1, стена Б; окно пом. 2, стена А; окно пом. 3, стена В; дверь пом. 3, стена Б; дверь пом. 4, стена В; и ещё 2); размер напечатан как принятый. Реестр: листы 7–9, вопросы К-1, К-8.
7. Номера помещений — по экспликации (лист 17); наименования и площади на этом листе не дублируются.
8. Марки текстиля «Т» и декора «Д» относятся только к листам текстиля и декора; индексы трубопроводов Т1–Т4 — на листах ВК и ОВ.

1000 мм · печать 1:1

Условные обозначения

- ковёр — габарит в масштабе, цвет изделия
- шина или карниз штор (выше плоскости разреза)
- портьеры (штора-волна)
- тюль (на плане — волнистая линия)
- римская или рулонная штора в проёме
- картина на стене — ширина в масштабе
- зеркало на стене — ширина в масштабе
- растение в кашпо — диаметр в масштабе
- ваза, настольный декор
- подушки, пледы — марки на мебели
- привязка от чистовой стены, мм
- (1) номер помещения, площадь м²
- стены (подложка обмера)
- * «*» — принято, не замерено и не подтверждено

Т1, ДК1 — марки по ведомостям текстиля и декора

Экспликация помещений

лист 17 · на плане — номера в марках

Окна: шина → полотно, мм

Поз.	Шина	Верх шины	Полотно, низ
Т13, Т14	3000	2800, ниша	2790, низ 10
Т15	1500	2500	1600, низ 900
Т7, Т8	2100	2900, ниша	2890, низ 10

Развеска: высоты от пола, мм

Поз.	Пом.	Ш×В	Центр	Низ	Стена
ДК3	3	550×450	1275	1050	Б
ДК5	5	600×1800	1450	550	А
ДК6	1	1000×800	1550	1150	Г
ДК9	4	500×700	1450	1100	А

Изм.	Кол.уч	Лист	№ док.	Подп.	Дата
Разраб.		Кырлан А.С.			04.11.26
Пров.					
ГИП					
Н. контр.					
Утв.					

ГД-2026-012-АИ

Дом 120 м²

Общая площадь 147,36* м² · * размеры приняты, не замерены (реестр — л. 7–9, К-1)

Дизайн-проект интерьера

Стадия	Лист	Листов
РП	89	175

План текстиля и декора · 1-й этаж

М 1:50


Кырлан Александр Сергеевич

выпуск 04.11.2026 № 4dfa962484 · стр. 91 из 180

План текстиля и декора · 2-й этаж

Шторы и карнизы, ковры, картины и зеркала, растения · размеры в мм от чистовых стен и чистого пола · марки — по ведомостям

ПРЕДВАРИТЕЛЬНО · не для производства работ · открыто пунктов: 11 (реестр — л. 7–9)

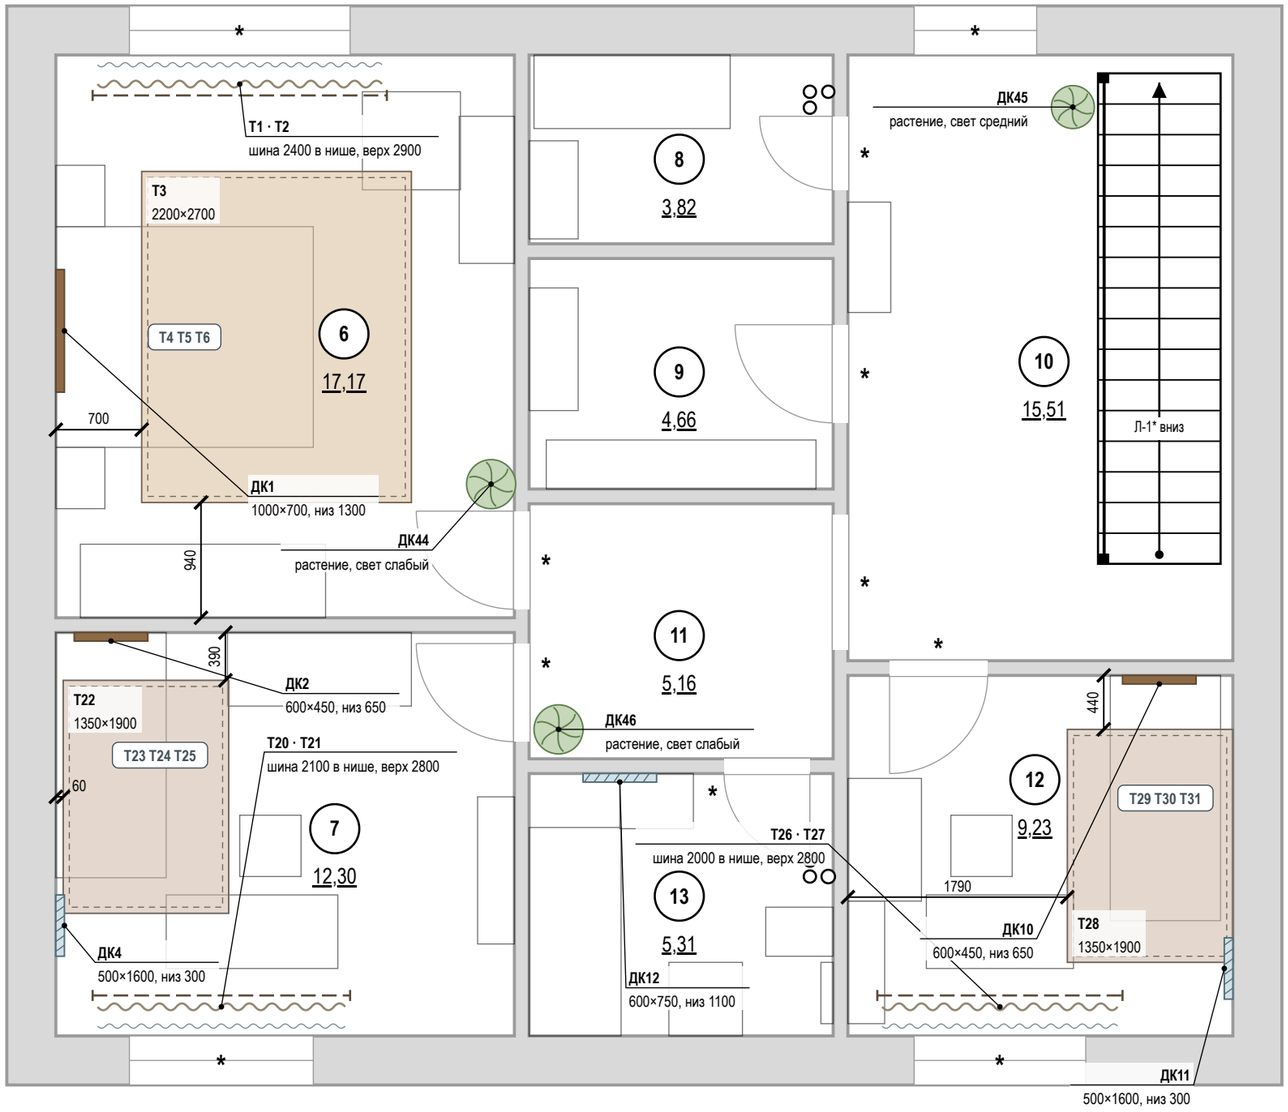

Условные обозначения

- ковёр — габарит в масштабе, цвет изделия
- шина или карниз штор (выше плоскости разреза)
- портьеры (штора-волна)
- тюль (на плане — волнистая линия)
- римская или рулонная штора в проёме
- картина на стене — ширина в масштабе
- зеркало на стене — ширина в масштабе
- растение в кашпо — диаметр в масштабе
- ваза, настольный декор
- подушки, пледы — марки на мебели
- привязка от чистовой стены, мм
- (1) номер помещения, площадь м²
- стены (подложка обмера)
- * «*» — принято, не замерено и не подтверждено

Т1, ДК1 — марки по ведомостям текстиля и декора

Экспликация помещений

лист 18 · на плане — номера в марках

Окна: шина → полотно, мм

Поз.	Шина	Верх шины	Полотно, низ
Т1, Т2	2400	2900, ниша	2890, низ 10
Т20, Т21	2100	2800, ниша	2790, низ 10
Т26, Т27	2000	2800, ниша	2790, низ 10

Развеска: высоты от пола, мм

Поз.	Пом.	Ш×В	Центр	Низ	Стена
ДК1	6	1000×700	1650	1300	Г
ДК2	7	600×450	875	650	А
ДК4	7	500×1600	1100	300	Г
ДК10	12	600×450	875	650	А
ДК11	12	500×1600	1100	300	Б
ДК12	13	600×750	1475	1100	А

Допущения и предложения на листе. Основа листа: взаимное расположение помещений, контур дома 9600 × 8000 и раскладка этажей подобраны проектировщиком под габариты помещений брифа; обмер и проект АР — задание (К-1); высота потолка 2900 мм — по брифу, не замерена; перекрытие 330 мм и отметка 2-го этажа +3,230 приняты; проект КР — задание (К-2); наружные стены 400 мм, перегородки 120 мм приняты (в брифе толщин нет) (К-1); разрешённая мощность 15 кВт принята по типовым ТУ для частного дома (К-4); подрайон климата не задан — принят не северный (жилые от 2,5 м) (К-7). Знак «*» — принято, не замерено (замерить): К-2: отметка чистого пола этажа «2-й этаж» +3,230; К-3: Л-1; К-5: Ст К1-1, Ст В1-1, Ст Т3-1, Ст К1-2 (кухня), Ст В1-2, Ст Т3-2. См. лист открытых вопросов (лист 7, записи К-1–К-5; лист 8, запись К-7).

Примечания

1. Размеры — в мм. Отступы ковров — от чистовых стен; высоты картин и зеркал — от чистого пола до центра или низа рамы.
2. Шторы — на шинах в нишах потолка (ниша — план потолков, лист 66); закладная под шину — до обшивки ГКЛ. Схемы окон, длины полотен и сборка — лист 91.
3. Картины и зеркала массой более 5 кг — на анкеры по основанию, нагрузка крепежа не меньше двойной массы изделия; на ГКЛ — только по закладной. Декор не перекрывает розетки и выключатели.
4. Ковры на гладком полу — на противоскользящей подложке.
5. Мебель — по плану расстановки мебели (лист 27); ведомость текстиля — лист 92, ведомость декора и схемы развески — лист 94.
6. Знак «*» у проёма — допущение: положение проёма не замерено (окно пом. 6, стена А; дверь пом. 6, стена Б; окно пом. 7, стена В; дверь пом. 7, стена Б; дверь пом. 8, стена Б; дверь пом. 9, стена Б; и ещё 5); размер напечатан как принятый. Реестр: листы 7–9, вопросы К-1, К-9.
7. Номера помещений — по экспликации (лист 18); наименования и площади на этом листе не дублируются.
8. Марки текстиля «Т» и декора «Д» относятся только к листам текстиля и декора; индексы трубопроводов Т1–Т4 — на листах ВК и ОВ.

1000 мм · печать 1:1

Изм.	Кол.уч	Лист	№ док.	Подп.	Дата
Разраб.		Кырлан А.С.			04.11.26
Пров.					
ГИП					
Н. контр.					
Утв.					

ГД-2026-012-АИ

Дом 120 м²

Общая площадь 147,36* м² · * размеры приняты, не замерены (реестр — л. 7–9, К-1)

Дизайн-проект интерьера

Стадия	Лист	Листов
РП	90	175

План текстиля и декора · 2-й этаж

М 1:50

Кырлан Александр Сергеевич

выпуск 04.11.2026 № 4dfa962484 · стр. 92 из 180

03

Декор и текстиль

Кырлан Александр Сергеевич


выпуск 04.11.2026 № 4dfa962484 · стр. 93 из 180

Шторы и карнизы


ПРЕДВАРИТЕЛЬНО · не для производства работ · открыто пунктов: 11 (реестр — л. 7–9)

Схемы окон «шина → полотно» (М 1:100) · отметки в м от ±0,000 (чистый пол 1-го этажа) · размеры в мм


Окно 1* — Гостиная-кухня (пом. 1): Т13, Т14 (М 1:100)

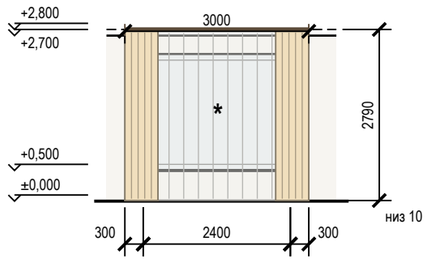


Окно 2* — Гостиная-кухня (пом. 1): Т15 (М 1:100)

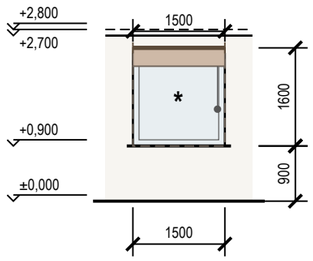


Окно 1* — Кабинет (пом. 3): Т7, Т8 (М 1:100)

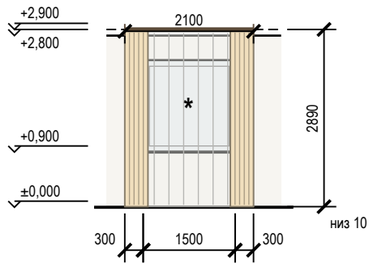


Окно 1* — Спальня родителей (пом. 6): Т1, Т2 (М 1:100)

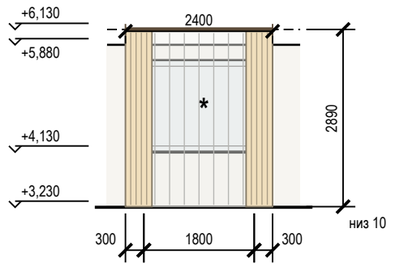

Окно 1* — Детская (пом. 7): Т20, Т21 (М 1:100)

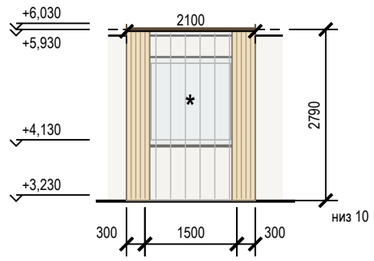

Окно 1* — Детская вторая (пом. 12): Т26, Т27 (М 1:100)

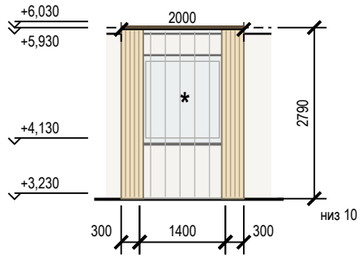

Карта окон: окно → шина → полотно

Поз.	Окно, пом.	Проём Ш×В, подоконник	Верх ниши	Изделие	Шина / карниз: длина, крепление	Верх шины	Полотно: длина, низ	Управление
Т13	1*, пом. 1	2400×1900, подок. 500	+2,800	портьеры	шина, 3000, в нише потолка, вынос 330	+2,800	2790, низ 10 (парит)	вручную
Т14	1*, пом. 1	2400×1900, подок. 500	+2,800	тюль	шина, 3000, в нише потолка, вынос 250	+2,800	2790, низ 10 (парит)	вручную
Т15	2*, пом. 1	1500×1500, подок. 900	+2,800	римская штора	карниз, 1500, на стену, вынос 60	+2,500	1600, низ 900	шнур, петля низом 1500, натяжитель
Т7	1*, пом. 3	1500×1500, подок. 900	+2,900	портьеры	шина, 2100, в нише потолка, вынос 330	+2,900	2890, низ 10 (парит)	вручную
Т8	1*, пом. 3	1500×1500, подок. 900	+2,900	тюль	шина, 2100, в нише потолка, вынос 250	+2,900	2890, низ 10 (парит)	вручную
Т1	1*, пом. 6	1800×1500, подок. 900	+6,130	портьеры	шина, 2400, в нише потолка, вынос 330	+6,130	2890, низ 10 (парит)	вручную
Т2	1*, пом. 6	1800×1500, подок. 900	+6,130	тюль	шина, 2400, в нише потолка, вынос 250	+6,130	2890, низ 10 (парит)	вручную
Т20	1*, пом. 7	1500×1450, подок. 900	+6,030	портьеры	шина, 2100, в нише потолка, вынос 330	+6,030	2790, низ 10 (парит)	вручную
Т21	1*, пом. 7	1500×1450, подок. 900	+6,030	тюль	шина, 2100, в нише потолка, вынос 250	+6,030	2790, низ 10 (парит)	вручную
Т26	1*, пом. 12	1400×1450, подок. 900	+6,030	портьеры	шина, 2000, в нише потолка, вынос 330	+6,030	2790, низ 10 (парит)	вручную
Т27	1*, пом. 12	1400×1450, подок. 900	+6,030	тюль	шина, 2000, в нише потолка, вынос 250	+6,030	2790, низ 10 (парит)	вручную

Условные обозначения

- портьеры в открытом положении
- римская штора: сложена / опущена
- верх ниши под шторы в потолке
- * — «*» — принято, не замерено и не подтверждено
- тюль (на виде окна — прозрачная плашка)
- шина или карниз на отметке верха
- оконный проём

Допущения и предложения на листе

Основа листа: взаимное расположение помещений, контур дома 9600 × 8000 и раскладка этажей подобраны проектировщиком под габариты помещений брифа; обмер и проект АР — задание (К-1); высота потолка 2900 мм — по брифу, не замерена; перекрытие 330 мм и отметка 2-го этажа +3,230 приняты; проект КР — задание (К-2); наружные стены 400 мм, перегородки 120 мм приняты (в брифе толщин нет) (К-1); разрешённая мощность 15 кВт принята по типовым ТУ для частного дома (К-4); подрайон климата не задан — принят не северный (жилые от 2,5 м) (К-7).

Знак «*» — принято, не замерено и не подтверждено (замерить на объекте): К-1: окно пом. 1 (стена А), 3 (В), 6 (А), 7 (В), 12 (В) — окно: место, ширина, высота и подоконник приняты по брифу, стена — по раскладке проектировщика (К-1), не замерены; дверь пом. 1 (стена Б), 3 (Б), 6 (Б), 7 (Б), 12 (А) — проём: место и ширина приняты проектировщиком по брифу (раскладка этажей — К-1), не замерены.

См. лист открытых вопросов (лист 7, записи К-1, К-2, К-4; лист 8, запись К-7).

Примечания

1. Отметки — в м от ±0,000 (чистый пол 1-го этажа); размеры — мм.
2. Шины в нишах потолка: закладная (брус или профиль) по всей длине ниши — до обшивки ГКЛ; ниша и её отметка — узел ниши на плане потолков (лист 66).
3. Шина в нише — на отметке верха ниши (крепление к закладной в потолке ниши); длина полотна — от верха шины до чистого пола за вычетом зазора.
4. Полотно портьер «парит» над полом на 10 мм; сборка портьер — 2,0, тюля — 2,5 (ширина полотна — в ведомости текстиля).
5. Шнур римской шторы — с натяжителем, петля низом не ниже 1500 мм от пола (защита детей; EN 13120 — рекомендация).
6. Электрокарнизы не предусмотрены; при замене на электропривод — вывод кабеля в нише у края шины (задание электрику).
7. Знак «*» у проёма — допущение: положение проёма не замерено (окно пом. 1, стена А (2 шт.); окно пом. 3, стена В; окно пом. 6, стена А; окно пом. 7, стена В; окно пом. 12, стена В); размер напечатан как принятый. Реестр: листы 7–9, вопросы К-1, К-8.
8. Длины шин и полотен окон 1 (пом. 1), 2 (пом. 1), 1 (пом. 3), 1 (пом. 6), 1 (пом. 7), 1 (пом. 12) выведены из размеров и положения проёма, а они — допущение: до раскроя полотен проём замерить, длины сверить.
9. Марки изделий — по плану текстиля и декора (лист 89) и ведомости текстиля (лист 92).

Изм.	Кол.уч	Лист	№ док.	Подп.	Дата
Разраб.		Кырлан А.С.			04.11.26
Пров.					
ГИП					
Н. контр.					
Утв.					

ГД-2026-012-АИ

Дом 120 м²

Общая площадь 147,36* м² · * размеры приняты, не замерены (реестр — л. 7–9, К-1)

Дизайн-проект интерьера

Стадия	Лист	Листов
РП	91	175

Шторы и карнизы

М б/м

Кырлан Александр Сергеевич

выпуск 04.11.2026 № 4dfa962484 · стр. 94 из 180

ПРЕДВАРИТЕЛЬНО · не для производства работ · открыто пунктов: 11 (реестр — л. 7–9)

Ведомость текстиля

Шторы, тюль, римские шторы, ковры, подушки и пледы · размеры в мм · марки — по плану текстиля и декора

Текстиль: шторы, ковры, подушки, пледы

Поз.	Пом.	Изделие	Размер, мм	Ткань, состав, плотность	Сборка, ширина полотна		Цвет (система, код)	Кол.	Примечание
T1	6	Портьеры-волна	шина 2400 × полотно 2890	лён с блэкаут-подкладкой; лён 100 %; 320 г/м²	× 2, ширина 5000		NCS S 1010-Y20R (Светлый песок / известняк)	2	низ 10 (парит); в нише потолка
T2	6	Тюль	шина 2400 × полотно 2890	вуаль; полиэстер 100 %	× 2,5, ширина 6250		Little Greene No. 222 (Loft White)	1	низ 10 (парит); в нише потолка
T3	6	Ковёр под кроватью	2200×2700	шерсть, ручное ткачество; шерсть 80 %, хлопок 20 %			Tikkurila X395	1	противоскользящая подложка; ворс 10 мм
T4	6	Подушки декоративные на кровать	500×500	лён 100 %			NCS S 1010-Y20R (Светлый песок / известняк)	3	на М1
T5	6	Подушки на кровать, акцент	400×600	хлопковый бархат 100 %			Farrow & Ball No. 89 (Lulworth Blue — светлая морская лазурь)	2	на М1
T6	6	Плед на кровать	1300×1700	шерсть мериноса 100 %			Farrow & Ball No. 89 (Lulworth Blue — светлая морская лазурь)	1	на М1
T7	3	Портьеры-волна	шина 2100 × полотно 2890	лён с блэкаут-подкладкой; лён 100 %; 320 г/м²	× 2, ширина 3640		NCS S 1010-Y20R (Светлый песок / известняк)	2	низ 10 (парит); в нише потолка
T8	3	Тюль	шина 2100 × полотно 2890	вуаль; полиэстер 100 %	× 2,5, ширина 4550		Little Greene No. 222 (Loft White)	1	низ 10 (парит); в нише потолка
T9	3	Ковёр под кроватью	2000×1500	шерсть, плоское плетение; шерсть 100 %			Tikkurila X463	1	противоскользящая подложка; ворс 8 мм
T10	3	Подушки декоративные на кровать	500×500	букле (шерсть 60 %, полиэстер 40 %)			NCS S 1010-Y20R (Светлый песок / известняк)	3	на К64
T11	3	Подушки на кровать, акцент	400×600	хлопковый бархат 100 %			NCS S 5020-G90Y (Олива)	2	на К64
T12	3	Плед на кровать	1300×1700	шерсть мериноса 100 %			NCS S 5020-G90Y (Олива)	1	на К64
T13	1	Портьеры-волна (гостиная)	шина 3000 × полотно 2790	лён 70 %, вискоза 30 %; 280 г/м²	× 2, ширина 4500		NCS S 1010-Y20R (Светлый песок / известняк)	2	низ 10 (парит); в нише потолка
T14	1	Тюль (гостиная)	шина 3000 × полотно 2790	вуаль; полиэстер 100 %	× 2,5, ширина 5625		Little Greene No. 222 (Loft White)	1	низ 10 (парит); в нише потолка
T15	1	Римская штора (кухня)	карниз 1500 × полотно 1600	лён 100 %			Tikkurila X463	1	низ 900; на стену; шнур: петля 1500, натяжитель
T16	1	Ковёр в зоне отдыха	2400×2000	шерсть, петля; шерсть 100 %			Tikkurila X463	1	противоскользящая подложка; ворс низкий
T17	1	Подушки на диван	500×500	букле (шерсть 60 %, полиэстер 40 %)			NCS S 1010-Y20R (Светлый песок / известняк)	3	на Гс2
T18	1	Подушки на диван, акцент	400×600	хлопковый бархат 100 %			NCS S 3050-R80B (Эгейский синий)	2	на Гс2
T19	1	Плед на диван	1300×1700	альпака 50 %, шерсть 50 %			Tikkurila X463	1	на Гс2
T20	7	Портьеры-волна	шина 2100 × полотно 2790	лён с блэкаут-подкладкой; лён 100 %; 320 г/м²	× 2, ширина 3640		NCS S 1010-Y20R (Светлый песок / известняк)	2	низ 10 (парит); в нише потолка
T21	7	Тюль	шина 2100 × полотно 2790	вуаль; полиэстер 100 %	× 2,5, ширина 4550		Little Greene No. 222 (Loft White)	1	низ 10 (парит); в нише потолка
T22	7	Ковёр под кроватью	1350×1900	шерсть, плоское плетение; шерсть 100 %			Tikkurila X463	1	противоскользящая подложка; ворс 8 мм
T23	7	Подушки декоративные на кровать	500×500	букле (шерсть 60 %, полиэстер 40 %)			NCS S 1010-Y20R (Светлый песок / известняк)	3	на Дт1
T24	7	Подушки на кровать, акцент	400×600	хлопковый бархат 100 %			Farrow & Ball No. 66 (India Yellow — охра / горчица итальянских фасадов)	2	на Дт1
T25	7	Плед на кровать	1300×1700	шерсть мериноса 100 %			Farrow & Ball No. 66 (India Yellow — охра / горчица итальянских фасадов)	1	на Дт1
T26	12	Портьеры-волна	шина 2000 × полотно 2790	лён с блэкаут-подкладкой; лён 100 %; 320 г/м²	× 2, ширина 3640		NCS S 1010-Y20R (Светлый песок / известняк)	2	низ 10 (парит); в нише потолка
T27	12	Тюль	шина 2000 × полотно 2790	вуаль; полиэстер 100 %	× 2,5, ширина 4550		Little Greene No. 222 (Loft White)	1	низ 10 (парит); в нише потолка
T28	12	Ковёр под кроватью	1350×1900	шерсть, плоское плетение; шерсть 100 %			Tikkurila X463	1	противоскользящая подложка; ворс 8 мм
T29	12	Подушки декоративные на кровать	500×500	букле (шерсть 60 %, полиэстер 40 %)			NCS S 1010-Y20R (Светлый песок / известняк)	3	на Дт6
T30	12	Подушки на кровать, акцент	400×600	хлопковый бархат 100 %			Tikkurila H440	2	на Дт6

Продолжение ведомости — на следующем листе; итог и примечания — на последнем листе ведомости.

Допущения и предложения на листе

Основа листа: взаимное расположение помещений, контур дома 9600 × 8000 и раскладка этажей подобраны проектировщиком под габариты помещений брифа; обмер и проект АР — задание (К-1); высота потолка 2900 мм — по брифу, не замерена; перекрытие 330 мм и отметка 2-го этажа +3,230 приняты; проект КР — задание (К-2); наружные стены 400 мм, перегородки 120 мм приняты (в брифе толщин нет) (К-1); разрешённая мощность 15 кВт принята по типовым ТУ для частного дома (К-4); подрайон климата не задан — принят не северный (жилые от 2,5 м) (К-7).

См. лист открытых вопросов (лист 7, записи К-1, К-2, К-4; лист 8, запись К-7).

Изм.	Кол.уч	Лист	№ док.	Подп.	Дата
Разраб.		Кырлан А.С.			04.11.26
Пров.					
ГИП					
Н. контр.					
Утв.					

ГД-2026-012-АИ

Дом 120 м²

Общая площадь 147,36* м² · * размеры приняты, не замерены (реестр — л. 7–9, К-1)

Дизайн-проект интерьера

Стадия	Лист	Листов
РП	92	175

Ведомость текстиля

М б/м

Кырлан Александр Сергеевич

выпуск 04.11.2026 № 4dfa962484 · стр. 95 из 180

Ведомость текстиля (продолжение)

Шторы, тюль, римские шторы, ковры, подушки и пледы · размеры в мм · марки — по плану текстиля и декора

Текстиль: шторы, ковры, подушки, пледы (продолжение)

Поз.	Пом.	Изделие	Размер, мм	Ткань, состав, плотность	Сборка, ширина полотна		Цвет (система, код)	Кол.	Примечание
T31	12	Плед на кровать	1300×1700	шерсть мериноса 100 %			Tikkurila H440	1	на Дт6

образец цвета — по HEX производителя краски, справочно

Итого: шторы и тюль — 16 шт.; ковры и дорожки — 5 шт.; подушки, пледы, покрывала — 30 шт.


Образцы по помещениям

1. Гостиная-кухня




T13 T14 T15 T16 T17 T18 T19

3. Кабинет

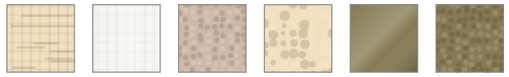


T7 T8 T9 T10 T11 T12

6. Спальня родителей

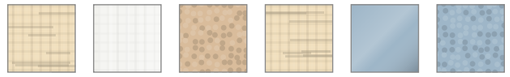

T1 T2 T3 T4 T5 T6

7. Детская

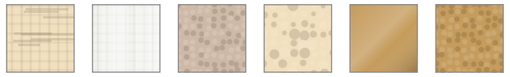

T20 T21 T22 T23 T24 T25

Примечания

1. Коды цвета — ориентир подбора по веерам производителей красок; ткань утверждается по образцу при дневном свете и при свете проекта 2700–3000 K.
2. Размеры полотен — по замеру после чистовой отделки пола и потолка; ширина полотна указана с учётом сборки, без припусков на швы. Схемы окон и отметки шин лист 91.
3. Портьеры и тюль — на тесьме «волна» по системе шины; блэкаут — подкладкой. Ковры — на противоскользящей подложке.
4. Замена изделия — аналогом по характеристикам (состав, плотность, размер, цвет по образцу) с согласованием автора проекта.
5. Места изделий — план текстиля и декора (лист 89); подушки и пледы — по марке мебели.

Допущения и предложения на листе

Основа листа: взаимное расположение помещений, контур дома 9600 × 8000 и раскладка этажей подобраны проектировщиком под габариты помещений брифа; обмер и проект АР — задание (К-1); высота потолка 2900 мм — по брифу, не замерена; перекрытие 330 мм и отметка 2-го этажа +3,230 приняты; проект КР — задание (К-2); наружные стены 400 мм, перегородки 120 мм приняты (в брифе толщин нет) (К-1); разрешённая мощность 15 кВт принята по типовым ТУ для частного дома (К-4); подрайон климата не задан — принят не северный (жилые от 2,5 м) (К-7).

См. лист открытых вопросов (лист 7, записи К-1, К-2, К-4; лист 8, запись К-7).

Изм.	Кол.уч	Лист	№ док.	Подп.	Дата
Разраб.		Кырлан А.С.			04.11.26
Пров.					
ГИП					
Н. контр.					
Утв.					

ГД-2026-012-АИ

Дом 120 м²

Общая площадь 147,36* м² · * размеры приняты, не замерены (реестр — л. 7–9, К-1)

Дизайн-проект интерьера

Стадия	Лист	Листов
РП	93	175

Ведомость текстиля (продолжение)

М б/м

Кырлан Александр Сергеевич

выпуск 04.11.2026 № 4dfa962484 · стр. 96 из 180

Ведомость декора. Схемы развески

ПРЕДВАРИТЕЛЬНО · не для производства работ · открыто пунктов: 11 (реестр — л. 7–9)


Картины, зеркала, растения, настольный декор · схемы развески (М 1:50) · высоты — мм от чистого пола

Декор: картины, зеркала, растения, предметы


картина · зеркало · мебель под изделием

Поз.	Пом.	Предмет	Размер, мм	Место: стена, высота от пола, мм	Масса, кг	Крепёж и основание	Свет места, отделка	Кол.
ДК1	6	Картина над кроватью: Ветви оливы с плодами, акварель на тёплой бумаге	1000×700	стена Г, привязка 1750; низ 1300, центр 1650; над М1	4	подвес по основанию, 2 точки	рама — дуб	1
ДК2	7	Картина над кроватью: Парусники в бухте, детская иллюстрация, гуашь	600×450	стена А, привязка 150; низ 650, центр 875; над Дт1	4	подвес по основанию, 2 точки	рама — дуб	1
ДК3	3	Картина над креслом: Старинная карта Эгейского моря, гравюра в паспарту	550×450	стена Б, привязка 240; низ 1050, центр 1275; над Кб4	4	подвес по основанию, 2 точки	рама — дуб	1
ДК4	7	Зеркало в рост в тонкой чёрной раме	500×1600	стена Г, привязка 2140; низ 300, центр 1100	12	анкер для пустотелых оснований, 4 шт.; основание: перегородка — определить обмером до монтажа; нагрузка 30 кг	рама — чёрный матовый металл	1
ДК5	5	Зеркало	600×1800	стена А, привязка 1840; низ 550, центр 1450	18	анкер, 4 шт.; основание: перегородка — определить обмером до монтажа; нагрузка 40 кг	рама — чёрный матовый металл	1
ДК6	1	Картина над креслом: Белые дома над бирюзовой бухтой, синие ставни, полдень; масло	1000×800	стена Г, привязка 700; центр 1550	6	анкер, 2 шт.; основание: перегородка — определить обмером до монтажа; нагрузка 15 кг		1
ДК7	1	Растение	450×450	напольное			свет средний	1
ДК8	1	Ваза керамическая с ветками на обеденном столе	200×350	на Кх15 (обеденный стол)				1
ДК9	4	Зеркало над умывальником, влагостойкое	500×700	стена А, привязка 640; низ 1100, центр 1450; над Cr2	4	подвес по основанию, 2 точки		1
ДК10	12	Картина над кроватью: Солнце и волны из цветных полукругов, детский принт	600×450	стена А, привязка 2240; низ 650, центр 875; над Дт6	4	подвес по основанию, 2 точки	рама — дуб	1
ДК11	12	Зеркало в рост в тонкой чёрной раме	500×1600	стена Б, привязка 2140; низ 300, центр 1100	12	анкер для пустотелых оснований, 4 шт.; основание: перегородка — определить обмером до монтажа; нагрузка 30 кг	рама — чёрный матовый металл	1
ДК12	13	Зеркало над умывальником, влагостойкое	600×750	стена А, привязка 440; низ 1100, центр 1475	4	подвес по основанию, 2 точки		1
ДК40	1	Олива в кадке Ø450 у окна	450×450	напольное			свет яркий рассеянный	1
ДК41	2	Сансевиерия в кашпо Ø400 под лестницей	400×400	напольное			свет слабый	1
ДК43	5	Замиокулькас в кашпо Ø350	350×350	напольное			свет слабый	1
ДК44	6	Аглаонема в кашпо Ø400	400×400	напольное			свет слабый	1
ДК45	10	Хлорофитум в кашпо Ø350 у окна	350×350	напольное			свет средний	1
ДК46	11	Сансевиерия в кашпо Ø400	400×400	напольное			свет слабый	1


ДК1 — Спальня родителей (пом. 6), стена Г (М 1:50)

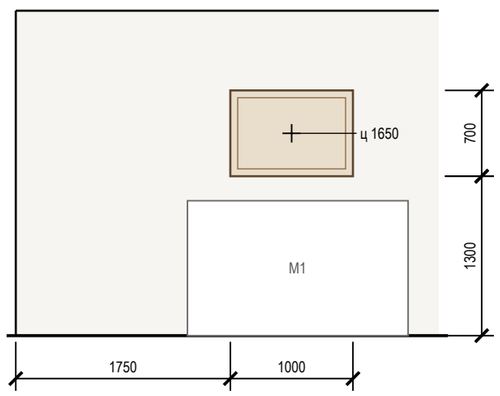

ДК2 — Детская (пом. 7), стена А (М 1:50)

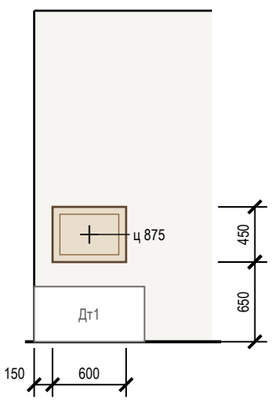

ДК3 — Кабинет (пом. 3), стена Б (М 1:50)

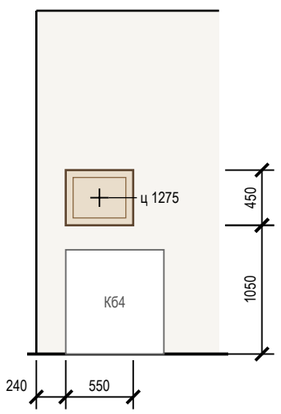

Допущения и предложения на листе

Основа листа: взаимное расположение помещений, контур дома 9600 × 8000 и раскладка этажей подобраны проектировщиком под габариты помещений брифа; обмер и проект АР — задание (К-1); высота потолка 2900 мм — по брифу, не замерена; перекрытие 330 мм и отметка 2-го этажа +3,230 приняты; проект КР — задание (К-2); наружные стены 400 мм, перегородки 120 мм приняты (в брифе толщин нет) (К-1); разрешённая мощность 15 кВт принята по типовым ТУ для частного дома (К-4); подрайон климата не задан — принят не северный (жилые от 2,5 м) (К-7). См. лист открытых вопросов (лист 7, записи К-1, К-2, К-4; лист 8, запись К-7).

Примечания

1. Высоты — от чистого пола помещения до низа изделия, «ц» — до центра; привязки — от чистовой грани угла стены, мм.
2. Над мебелью низ изделия — на 150–250 мм выше спинки или изголовья; без мебели центр — на 1450–1600 мм от пола.
3. Изделия до 5 кг — на два подвеса по основанию; тяжелее — на анкеры с нагрузкой не меньше двойной массы; на ГКЛ — только по закладной или анкеру для пустотелых оснований.
4. Зеркала в рост — с креплением от опрокидывания; в санузлах — влагостойкие, на клей для зеркал и нейтральный силикон.
5. Места изделий — план текстиля и декора (лист 89). Схемы развески остальных изделий — лист 95.

Изм.	Кол.уч	Лист	№ док.	Подп.	Дата
Разраб.		Кырлан А.С.			04.11.26
Пров.					
ГИП					
Н. контр.					
Утв.					

ГД-2026-012-АИ

Дом 120 м²

Общая площадь 147,36* м² · * размеры приняты, не замерены (реестр — л. 7–9, К-1)

Дизайн-проект интерьера

Стадия	Лист	Листов
РП	94	175

Ведомость декора. Схемы развески

М б/м

Кырлан Александр Сергеевич

выпуск 04.11.2026 № 4dfa962484 · стр. 97 из 180

Схемы развески (продолжение)


Схемы развески картин и зеркал (М 1:50) · высоты — мм от чистого пола

ПРЕДВАРИТЕЛЬНО · не для производства работ · открыто пунктов: 11 (реестр — л. 7–9)


Ведомость декора (размер, масса, крепёж и основание) — лист 94

картина · зеркало · мебель под изделием


ДК4 — Детская (пом. 7), стена Г (М 1:50)

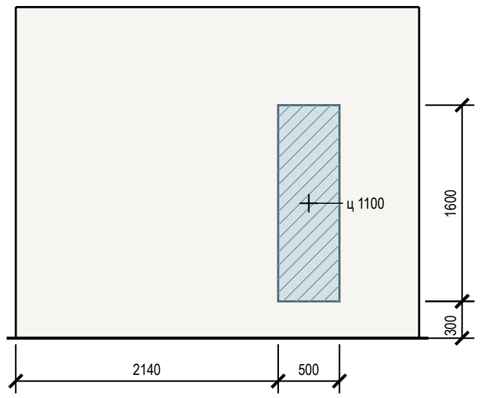


ДК5 — Прихожая (пом. 5), стена А (М 1:50)

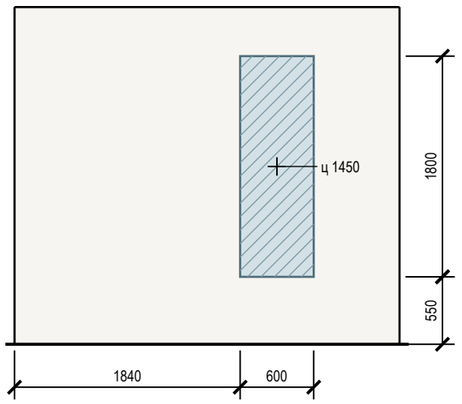


ДК6 — Гостиная-кухня (пом. 1), стена Г (М 1:50)

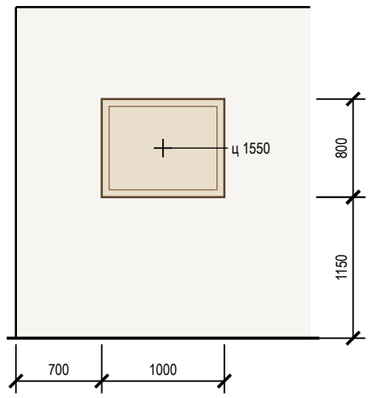


ДК9 — Санузел гостевой (пом. 4), стена А (М 1:50)

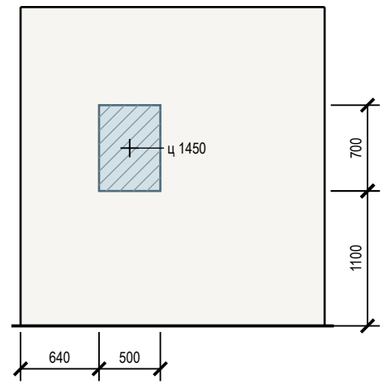


ДК10 — Детская вторая (пом. 12), стена А (М 1:50)

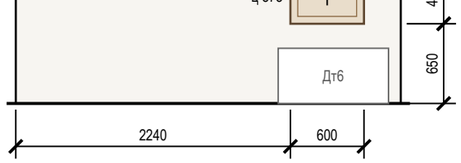

ДК11 — Детская вторая (пом. 12), стена Б (М 1:50)

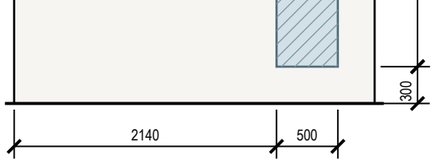

ДК12 — Санузел второго этажа (пом. 13), стена А (М 1:50)

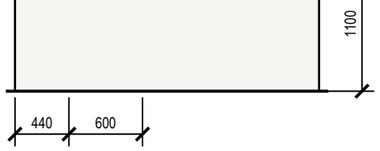

Допущения и предложения на листе

Основа листа: взаимное расположение помещений, контур дома 9600 × 8000 и раскладка этажей подобраны проектировщиком под габариты помещений брифа; обмер и проект АР — задание (К-1); высота потолка 2900 мм — по брифу, не замерена; перекрытие 330 мм и отметка 2-го этажа +3,230 приняты; проект КР — задание (К-2); наружные стены 400 мм, перегородки 120 мм приняты (в брифе толщин нет) (К-1); разрешённая мощность 15 кВт принята по типовым ТУ для частного дома (К-4); подрайон климата не задан — принят не северный (жилые от 2,5 м) (К-7). См. лист открытых вопросов (лист 7, записи К-1, К-2, К-4; лист 8, запись К-7).

Примечания

1. Высоты — от чистого пола помещения до низа изделия, «ц» — до центра; привязки — от чистовой грани угла стены, мм.
2. Над мебелью низ изделия — на 150–250 мм выше спинки или изголовья; без мебели центр — на 1450–1600 мм от пола.
3. Изделия до 5 кг — на два подвеса по основанию; тяжелее — на анкеры с нагрузкой не меньше двойной массы; на ГКЛ — только по закладной или анкеру для пустотелых оснований.
4. Зеркала в рост — с креплением от опрокидывания; в санузлах — влагостойкие, на клей для зеркал и нейтральный силикон.
5. Места изделий — план текстиля и декора (лист 89). Ведомость декора: размер, масса, крепёж и основание — лист 94.

Изм.	Кол.уч	Лист	№ док.	Подп.	Дата
Разраб.		Кырлан А.С.			04.11.26
Пров.					
ГИП					
Н. контр.					
Утв.					

ГД-2026-012-АИ

Дом 120 м²

Общая площадь 147,36* м² · * размеры приняты, не замерены (реестр — л. 7–9, К-1)

Дизайн-проект интерьера

Стадия	Лист	Листов
РП	95	175

Схемы развески (продолжение)

М б/м


Кырлан Александр Сергеевич

выпуск 04.11.2026 № 4dfa962484 · стр. 98 из 180

Встроенная мебель. Схема расположения · 1-й этаж

встроенная и корпусная мебель на заказ, кухонный гарнитур · размеры в мм · марки — по ведомости изделий

ПРЕДВАРИТЕЛЬНО · не для производства работ · открыто пунктов: 11 (реестр — л. 7–9)

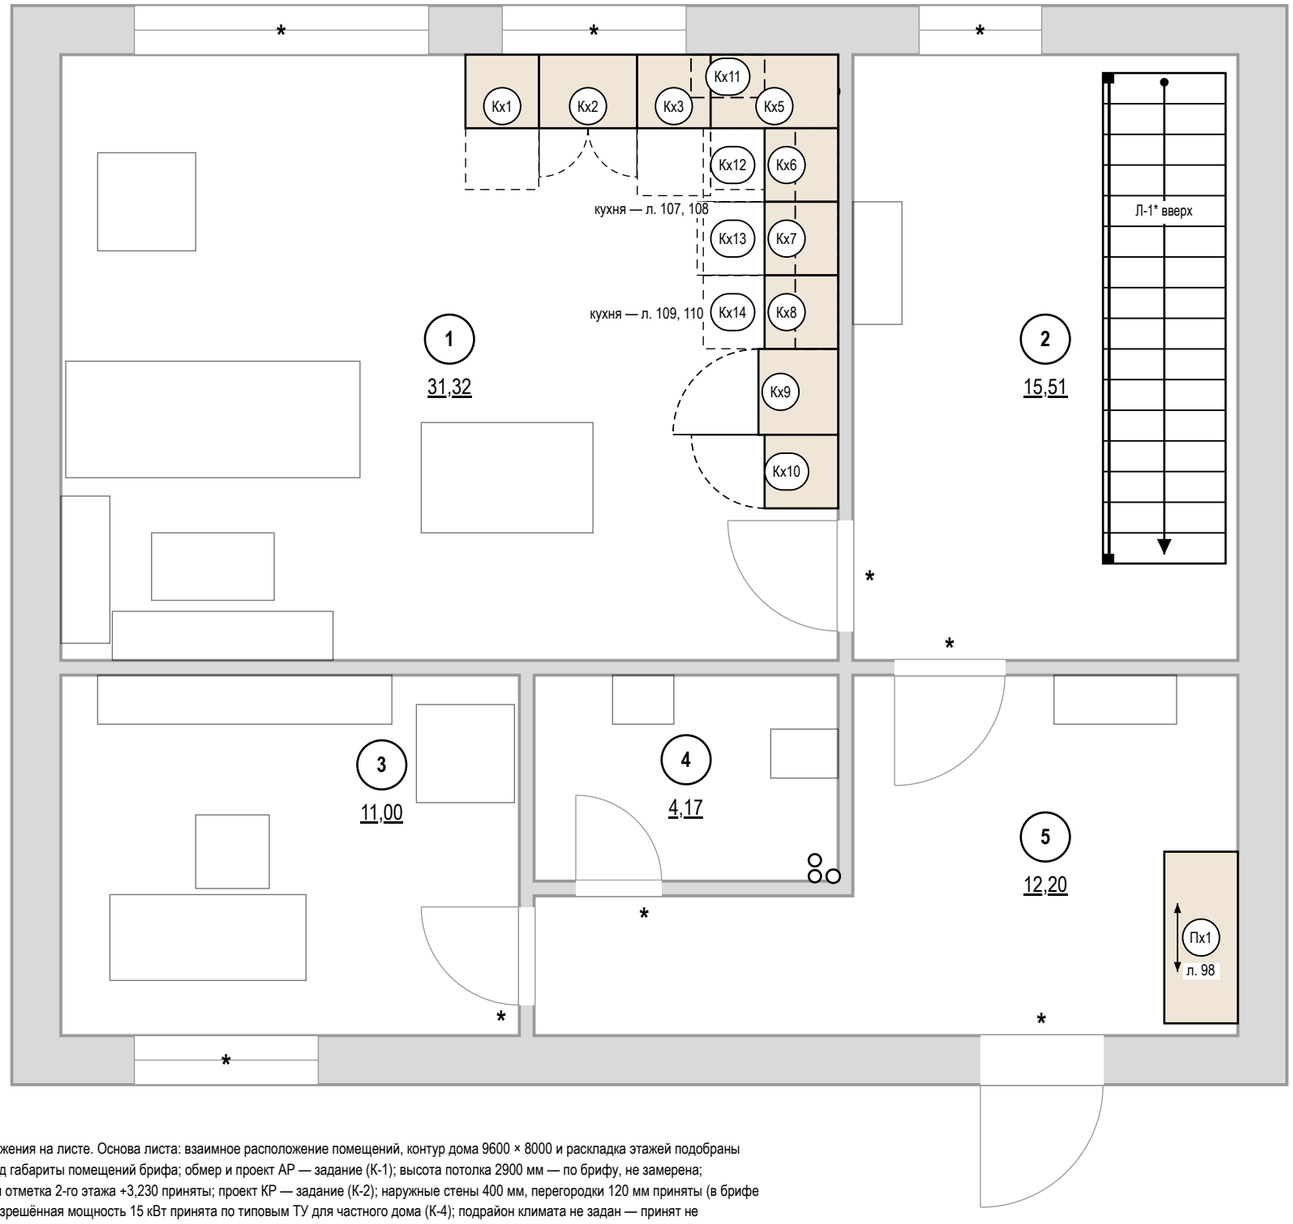

Допущения и предложения на листе. Основа листа: взаимное расположение помещений, контур дома 9600 × 8000 и раскладка этажей подобраны проектировщиком под габариты помещений брифа; обмер и проект АР — задание (К-1); высота потолка 2900 мм — по брифу, не замерена; перекрытие 330 мм и отметка 2-го этажа +3,230 приняты; проект КР — задание (К-2); наружные стены 400 мм, перегородки 120 мм приняты (в брифе толщин нет) (К-1); разрешённая мощность 15 кВт принята по типовым ТУ для частного дома (К-4); подрайон климата не задан — принят не северный (жилые от 2,5 м) (К-7). Знак «*» — принято, не замерено и не подтверждено (замерить на объекте): К-3: Л-1 — место, тип и размеры лестницы брифом не заданы (только «лестница из холла 1-го этажа»): одномаршевая 17 × 190 × 250 вдоль стены Б холла — предложение проектировщика; конструкция и расчёт — проект КР; К-5: Ст К1-1, Ст В1-1, Ст Т3-1, Ст К1-2 (кухня), Ст В1-2, Ст Т3-2 — положение стояка принято проектировщиком (проект ВК дома не передан), не замерено. См. лист открытых вопросов (лист 7, записи К-1–К-5; лист 8, запись К-7).

Примечания

1. Изделия — по чистовым размерам помещений; перед раскроем — контрольный замер цеха после чистовой отделки стен, пола и потолка.
2. Открывание фасадов и выдвижение ящиков показано в открытом положении: зоны не пересекают двери, радиаторы, выключатели и проходы.
3. Стояки и счётчики за мебелью — с сервисным люком; газовые трубы мебелью не зашиваются.
4. Покупная мебель — по плану расстановки мебели и спецификации дизайнера; здесь — подложкой.
5. Знак «*» у проёма — положение не замерено; реестр: листы 7–9, вопросы К-1, К-8.

1000 мм · печать 1:1

Ведомость изделий

Марка	Наименование	Пом.	Ш×Г×В, мм	Лист
Пх1	Шкаф-купе	5	1400×600×2650	98
Кх1	Модуль нижний: ящики	1	600×600×900	107
Кх2	Модуль нижний: мойка	1	800×600×900	107
Кх3	Модуль под ПММ 60: без корпуса, фасад на дверь машины	1	600×600×900	107
Кх11	Модуль навесной: полки	1	600×350×900	107
Кх5	Модуль нижний: ящики	1	1040×600×900	107
Кх6	Модуль нижний: ящики	1	600×600×900	109
Кх12	Модуль навесной: полки	1	600×350×900	109
Кх7	Модуль нижний: духовой шкаф, варочная	1	600×600×900	109
Кх13	Модуль навесной: полки	1	600×350×800	109
Кх8	Модуль нижний: ящики	1	600×600×900	109
Кх14	Модуль навесной: полки	1	600×350×900	109
Кх9	Пенал: холодильник встр.	1	700×650×2200	109
Кх10	Пенал: полки	1	600×600×2200	109

Условные обозначения

- изделие мебельщика: корпус на полу
- невидимый контур: навесной модуль, корпус под столешницей
- открывание распашного фасада
- зона выдвижения ящика, двери техники
- дверь купе, стрелка — направление движения
- К1 — марка изделия или модуля (на схеме расположения под ней — лист изделия)
- * — «*» — принято, не замерено и не подтверждено

Изм.	Кол.уч	Лист	№ док.	Подп.	Дата
Разраб.		Кырлан А.С.			04.11.26
Пров.					
ГИП					
Н. контр.					
Утв.					

ГД-2026-012-АИ

Дом 120 м²

Общая площадь 147,36* м² · * размеры приняты, не замерены (реестр — л. 7–9, К-1)

Дизайн-проект интерьера

Стадия	Лист	Листов
РП	96	175

Встроенная мебель. Схема расположения · 1-й этаж

М 1:50


Кырлан Александр Сергеевич

выпуск 04.11.2026 № 4dfa962484 · стр. 99 из 180

Встроенная мебель. Схема расположения · 2-й этаж

встроенная и корпусная мебель на заказ, кухонный гарнитур · размеры в мм · марки — по ведомости изделий

ПРЕДВАРИТЕЛЬНО · не для производства работ · открыто пунктов: 11 (реестр — л. 7–9)

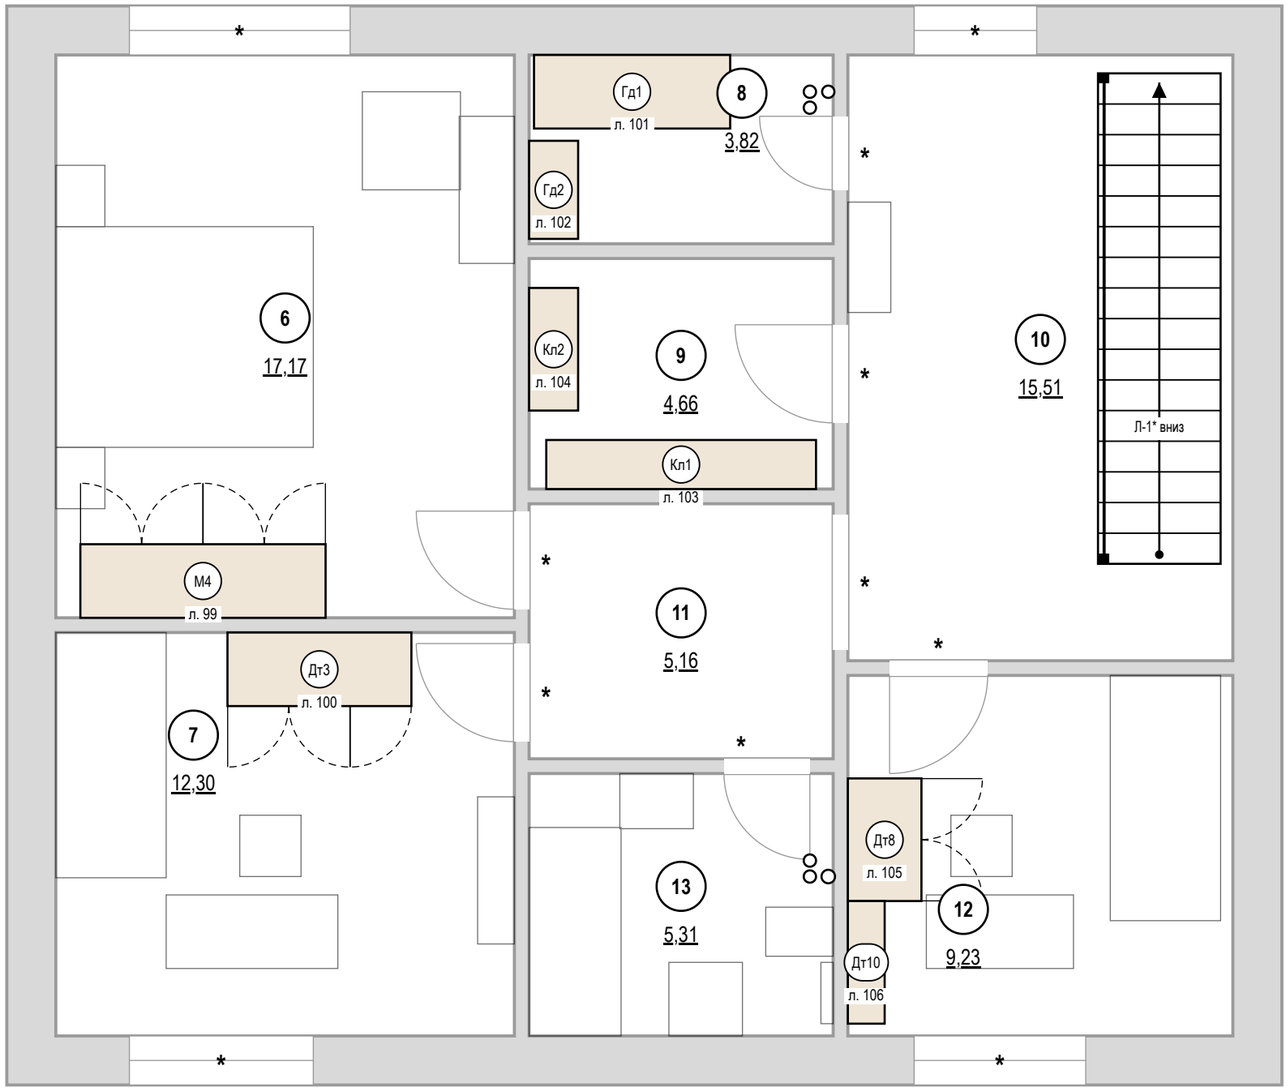

Ведомость изделий

Марка	Наименование	Пом.	Ш×Г×В, мм	Лист
М4	Шкаф распашной	6	2000×600×2600	99
Дт3	Шкаф распашной	7	1500×600×2200	100
Гд1	Система хранения	8	1600×600×2600	101
Гд2	Система хранения	8	800×400×2000	102
Кл1	Система хранения	9	2200×400×2200	103
Кл2	Система хранения	9	1000×400×2200	104
Дт8	Шкаф распашной	12	1000×600×2200	105
Дт10	Система хранения	12	1000×300×1200	106

Условные обозначения

- изделие мебельщика: корпус на полу
- невидимый контур: навесной модуль, корпус под столешницей
- открывание распашного фасада
- зона выдвижения ящика, двери техники
- дверь купе, стрелка — направление движения
- К1 — марка изделия или модуля (на схеме расположения под ней — лист изделия)
- * — «*» — принято, не замерено и не подтверждено

Допущения и предложения на листе

Основа листа: взаимное расположение помещений, контур дома 9600 × 8000 и раскладка этажей подобраны проектировщиком под габариты помещений брифа; обмер и проект АР — задание (К-1); высота потолка 2900 мм — по брифу, не замерена; перекрытие 330 мм и отметка 2-го этажа +3,230 приняты; проект КР — задание (К-2); наружные стены 400 мм, перегородки 120 мм приняты (в брифе толщин нет) (К-1); разрешённая мощность 15 кВт принята по типовым ТУ для частного дома (К-4); подрайон климата не задан — принят не северный (жилые от 2,5 м) (К-7).

Знак «*» — принято, не замерено и не подтверждено (замерить на объекте): К-1: окно пом. 6 (стена А), 7 (В), 10 (А), 12 (В) — окно: место, ширина, высота и подоконник приняты по брифу, стена — по раскладке проектировщика (К-1), не замерены; дверь пом. 6 (стена Б), 7 (Б), 8 (Б), 9 (Б), 11 (Б), 12 (А) — проём: место и ширина приняты проектировщиком по брифу (раскладка этажей — К-1), не замерены; дверь пом. 13 (стена А) — Петли у правого откоса (х 6150, у стояков): открытое полотно стоит вдоль стены Б, вошедший идёт влево к умывальнику и ванне; К-2: отметка чистого пола этажа «2-й этаж» +3,230 — отметка чистого пола 2-го этажа +3,230 принята: высота потолка 2900 по брифу + перекрытие с полом 330 (конструкция перекрытия не задана; проект КР — задание); К-3: Л-1 — место, тип и размеры лестницы брифом не заданы (только «лестница из холла 1-го этажа»): одномаршевая 17 × 190 × 250 вдоль стены Б холла — предложение проектировщика; конструкция и расчёт — проект КР; К-5: Ст К1-1, Ст В1-1, Ст Т3-1, Ст К1-2 (кухня), Ст В1-2, Ст Т3-2 — положение стояка принято проектировщиком (проект ВК дома не передан), не замерено.

См. лист открытых вопросов (лист 7, записи К-1–К-5; лист 8, запись К-7).

Примечания

1. Изделия — по чистовым размерам помещений; перед раскроем — контрольный замер цеха после чистовой отделки стен, пола и потолка.
2. Открывание фасадов и выдвижение ящиков показано в открытом положении: зоны не пересекают двери, радиаторы, выключатели и проходы.
3. Стояки и счётчики за мебелью — с сервисным люком; газовые трубы мебелью не зашиваются.
4. Покупная мебель — по плану расстановки мебели и спецификации дизайнера; здесь — подложкой.
5. Знак «*» у проёма — положение не замерено; реестр: листы 7–9, вопросы К-1, К-9.

1000 мм · печать 1:1

Изм.	Кол.уч	Лист	№ док.	Подп.	Дата
Разраб.		Кырлан А.С.			04.11.26
Пров.					
ГИП					
Н. контр.					
Утв.					

ГД-2026-012-АИ

Дом 120 м²

Общая площадь 147,36* м² · * размеры приняты, не замерены (реестр — л. 7–9, К-1)

Дизайн-проект интерьера

Стадия	Лист	Листов
РП	97	175

Встроенная мебель. Схема расположения · 2-й этаж

М 1:50

Кырлан Александр Сергеевич


выпуск 04.11.2026 № 4dfa962484 · стр. 100 из 180

Шкаф-купе Пх1


Прихожая (пом. 5) · вид из помещения · размеры в мм, отметки в м от ±0,000 (чистый пол 1-го этажа)

ПРЕДВАРИТЕЛЬНО · не для производства работ · открыто пунктов: 11 (реестр — л. 7–9)


Вид с фасадами

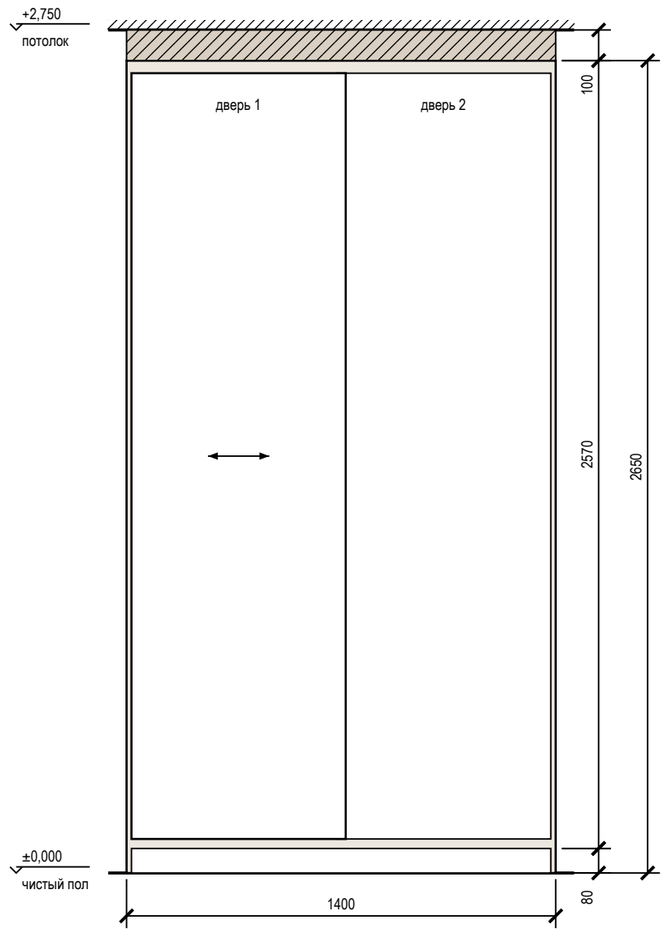


Вид без фасадов

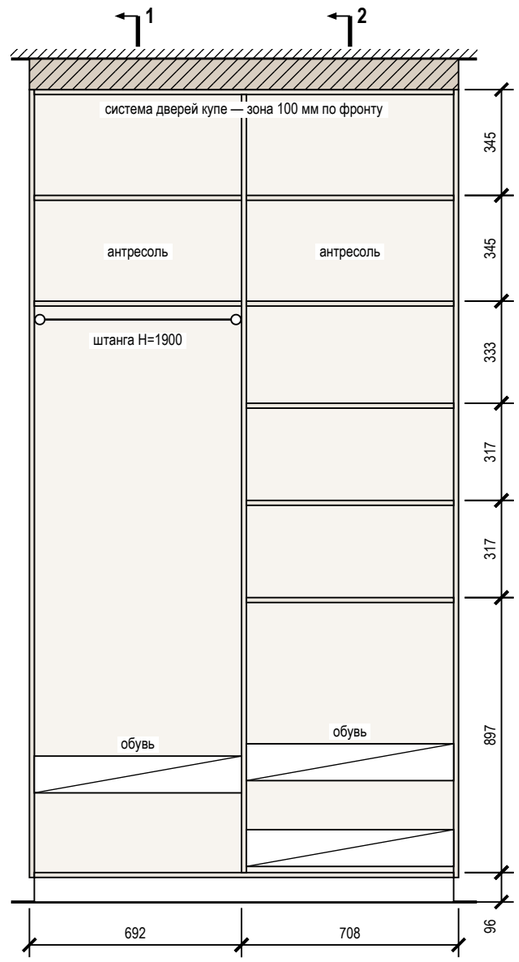

Разрез 1-1

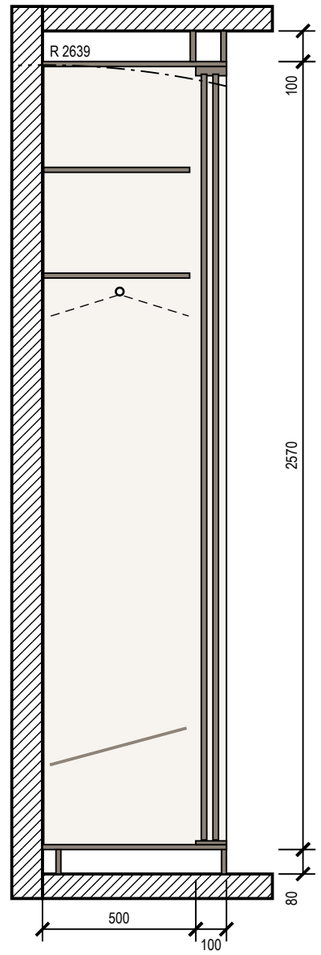

Разрез 2-2

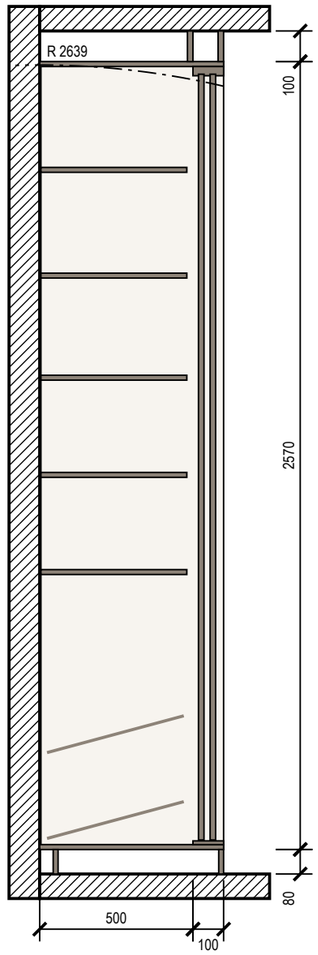

Примечания

1. Размеры — в мм по чистовой отделке; изделие 1400×600×2650 (Ш×Г×В). Перед раскроем — контрольный замер цеха после чистовой отделки стен, пола и потолка.
2. Корпус — ЛДСП 16 мм, задняя стенка ХДФ 4 мм в паз, цоколь 80 мм на регулируемых опорах; двери купе — ЛДСП 10 мм в алюминиевом профиле; нахлёст 30 мм, ширина двери 699 мм, высота — проём минус 40 мм; цвет — по колерной карте.
3. Кромка: скрытые торцы 0,4 мм, видимые 2 мм (ПВХ/АБС).
4. Номинальные зазоры: дверь купе — боковина 3 мм, фасад ящика — стойка 2 мм; ящики внутри купе — с накладкой 30 мм на стойке со стороны нахлёста дверей.
5. Присадка по 32-й системе — выполняет цех.
6. Компенсатор 100 мм — короб из ЛДСП по фронту и торцам, подгоняется к потолку при монтаже (припуск 20 мм), крепится к корпусу и к потолку.
7. Подъём корпуса: диагональ боковины без цоколя √(2570² + 600²) = 2639 мм < 2750 мм до потолка — корпус собирается лёжа, поднимается поворотом и ставится на цоколь.
8. Крепление к стене от опрокидывания — уголки 2 шт. к несущему основанию (монтажная схема шкафов).

Условные обозначения

- дверь купе, стрелка — направление движения
- корпус и полки ЛДСП (вид на стену)
- задняя стенка ХДФ
- деталь в разрезе
- компенсатор — короб до потолка
- штанга для плечиков (на разрезе — плечики 450 мм)
- траектория угла корпуса при подъёме в проектное положение

Допущения и предложения на листе

Основа листа: взаимное расположение помещений, контур дома 9600 × 8000 и раскладка этажей подобраны проектировщиком под габариты помещений брифа; обмер и проект АР — задание (К-1); высота потолка 2900 мм — по брифу, не замерена; перекрытие 330 мм и отметка 2-го этажа +3,230 приняты; проект КР — задание (К-2); наружные стены 400 мм, перегородки 120 мм приняты (в брифе толщин нет) (К-1); разрешённая мощность 15 кВт принята по типовым ТУ для частного дома (К-4); подрайон климата не задан — принят не северный (жилые от 2,5 м) (К-7).
См. лист открытых вопросов (лист 7, записи К-1, К-2, К-4; лист 8, запись К-7).

1000 мм · печать 1:1

Изм.	Кол.уч	Лист	№ док.	Подп.	Дата
Разраб.		Кырлан А.С.			04.11.26
Пров.					
ГИП					
Н. контр.					
Утв.					

ГД-2026-012-АИ

Дом 120 м²

Общая площадь 147,36* м² · * размеры приняты, не замерены (реестр — л. 7–9, К-1)

Дизайн-проект интерьера

Стадия	Лист	Листов
РП	98	175

Шкаф-купе Пх1

М 1:20

Кырлан Александр Сергеевич


выпуск 04.11.2026 № 4dfa962484 · стр. 101 из 180

Шкаф распашной М4


Спальня родителей (пом. 6) · вид из помещения · размеры в мм, отметки в м от ±0,000 (чистый пол 1-го этажа)

ПРЕДВАРИТЕЛЬНО · не для производства работ · открыто пунктов: 11 (реестр — л. 7–9)


Вид с фасадами

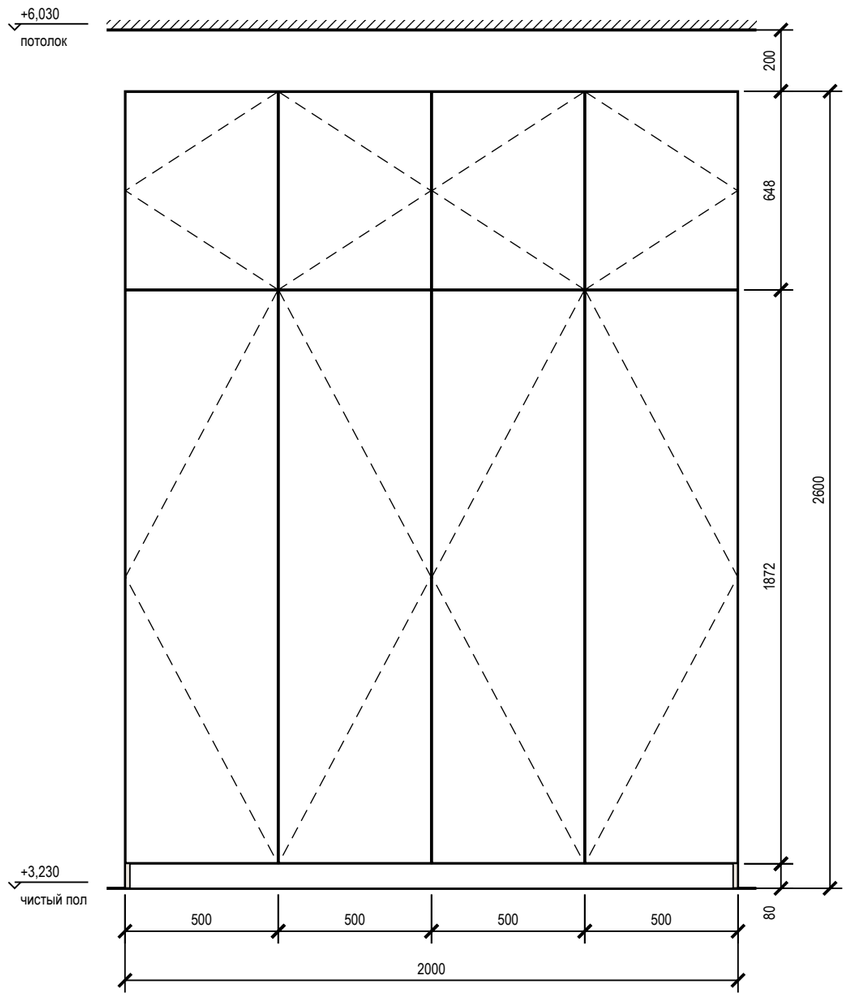


Вид без фасадов

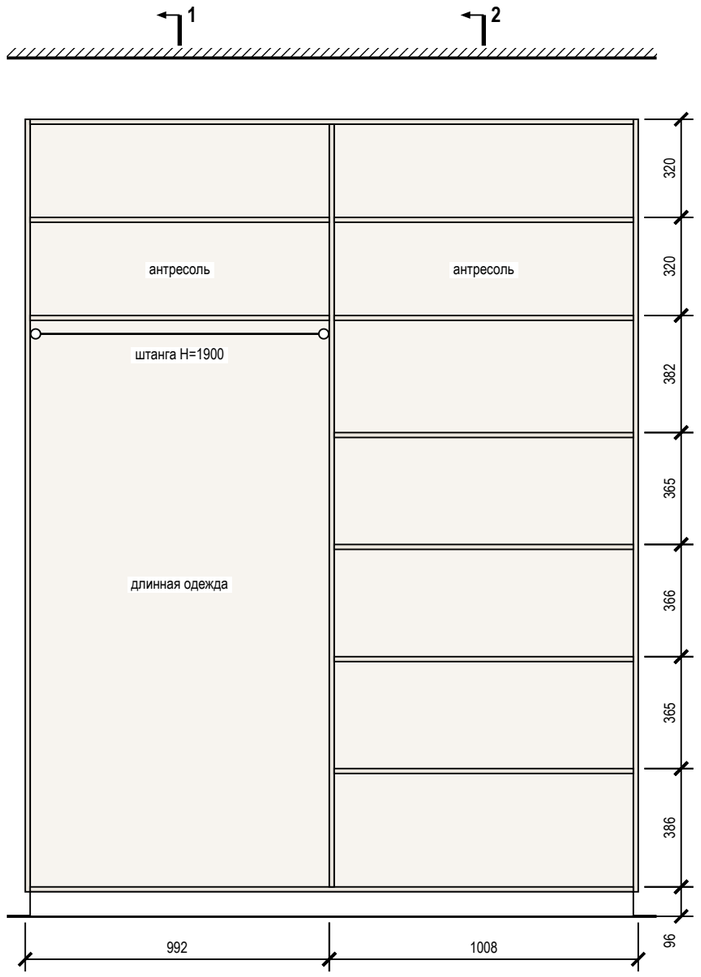

Разрез 1-1

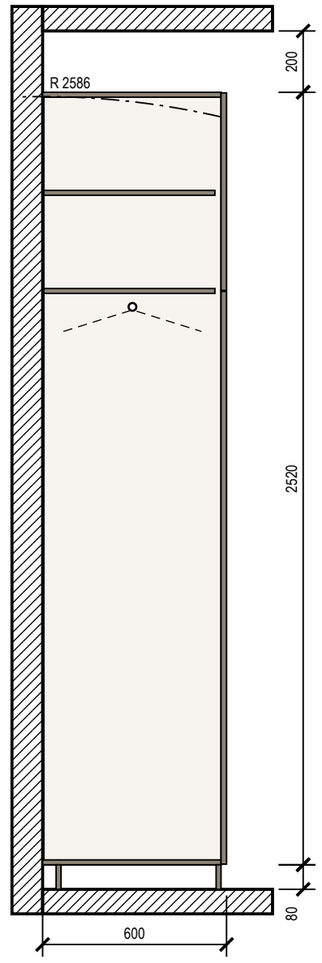

Разрез 2-2

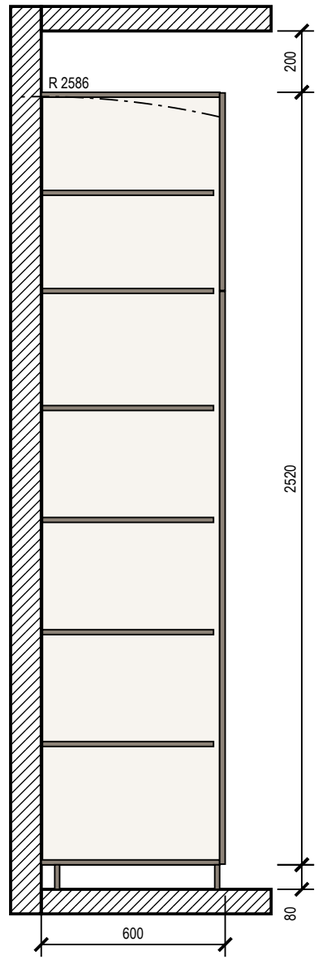

Примечания

1. Размеры — в мм по чистовой отделке; изделие 2000×600×2600 (Ш×Г×В). Перед раскроем — контрольный замер цеха после чистовой отделки стен, пола и потолка.
2. Корпус — ЛДСП 16 мм, задняя стенка ХДФ 4 мм в паз, цоколь 80 мм на регулируемых опорах; фасады накладные — МДФ 18 мм, эмаль матовая, 18 мм; цвет — по колерной карте; петли с доводчиком: фасад 1869 мм — 4 петли, фасад 645 мм — 2 петли.
3. Кромка: скрытые торцы 0,4 мм, видимые 2 мм (ПВХ/АБС).
4. Номинальные зазоры: между фасадами 3 мм, фасад — стена и фасад — потолок не менее 3 мм, фасад ящика — стойка 2 мм.
5. Присадка по 32-й системе — выполняет цех.
6. Зазор до потолка 200 мм.
7. Подъём корпуса: диагональ боковины без цоколя $\sqrt{(2520^2 + 582^2)} = 2586$ мм < 2800 мм до потолка — корпус собирается лёжа, поднимается поворотом и ставится на цоколь.
8. Крепление к стене от опрокидывания — уголки 2 шт. к несущему основанию (монтажная схема шкафов).

Условные обозначения

- фасад распашной: линии сходятся к стороне петель
- корпус и полки ЛДСП (вид на стену)
- задняя стенка ХДФ
- деталь в разрезе
- штанга для плечиков (на разрезе — плечики 450 мм)
- траектория угла корпуса при подъёме в проектное положение

Допущения и предложения на листе

Основа листа: взаимное расположение помещений, контур дома 9600 × 8000 и раскладка этажей подобраны проектировщиком под габариты помещений брифа; обмер и проект АР — задание (К-1); высота потолка 2900 мм — по брифу, не замерена; перекрытие 330 мм и отметка 2-го этажа +3,230 приняты; проект КР — задание (К-2); наружные стены 400 мм, перегородки 120 мм приняты (в брифе толщин нет) (К-1); разрешённая мощность 15 кВт принята по типовым ТУ для частного дома (К-4); подрайон климата не задан — принят не северный (жилые от 2,5 м) (К-7).

Знак «*» — принято, не замерено и не подтверждено (замерить на объекте): К-2: отметка чистого пола этажа «2-й этаж» +3,230 — отметка чистого пола 2-го этажа +3,230 принята: высота потолка 2900 по брифу + перекрытие с полом 330 (конструкция перекрытия не задана; проект КР — задание).

См. лист открытых вопросов (лист 7, записи К-1, К-2, К-4; лист 8, запись К-7).

1000 мм · печать 1:1

Изм.	Кол.уч	Лист	№ док.	Подп.	Дата
Разраб.		Кырлан А.С.			04.11.26
Пров.					
ГИП					
Н. контр.					
Утв.					

ГД-2026-012-АИ

Дом 120 м²

Общая площадь 147,36* м² · * размеры приняты, не замерены (реестр — л. 7–9, К-1)

Дизайн-проект интерьера

Стадия	Лист	Листов
РП	99	175

Шкаф распашной М4

М 1:20


Кырлан Александр Сергеевич

выпуск 04.11.2026 № 4dfa962484 · стр. 102 из 180


Шкаф распашной Дт3

Детская (пом. 7) · вид из помещения · размеры в мм, отметки в м от ±0,000 (чистый пол 1-го этажа)


Вид с фасадами

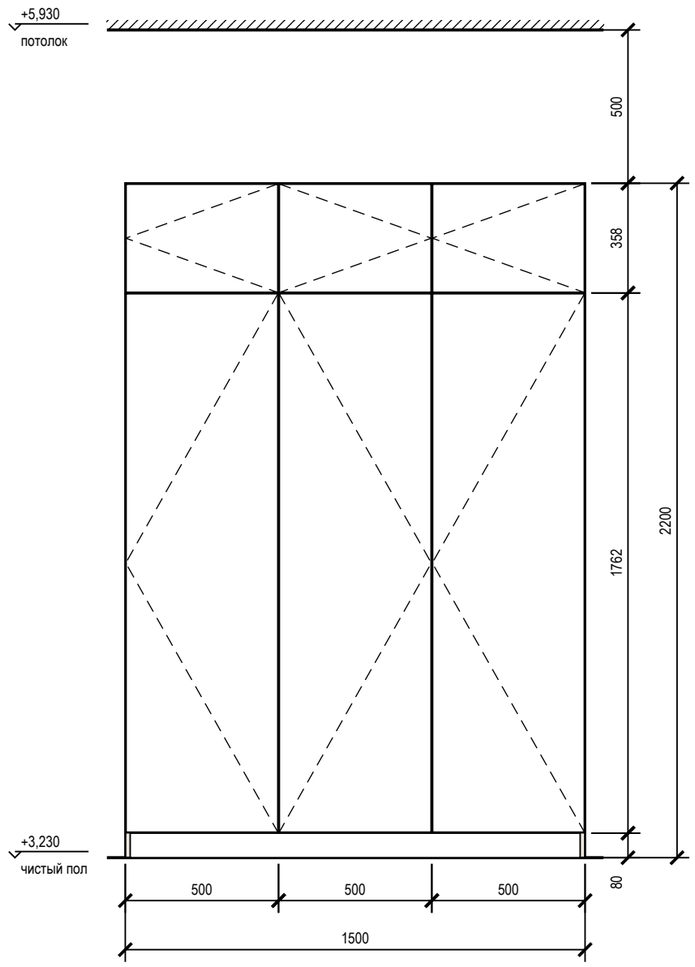


Вид без фасадов

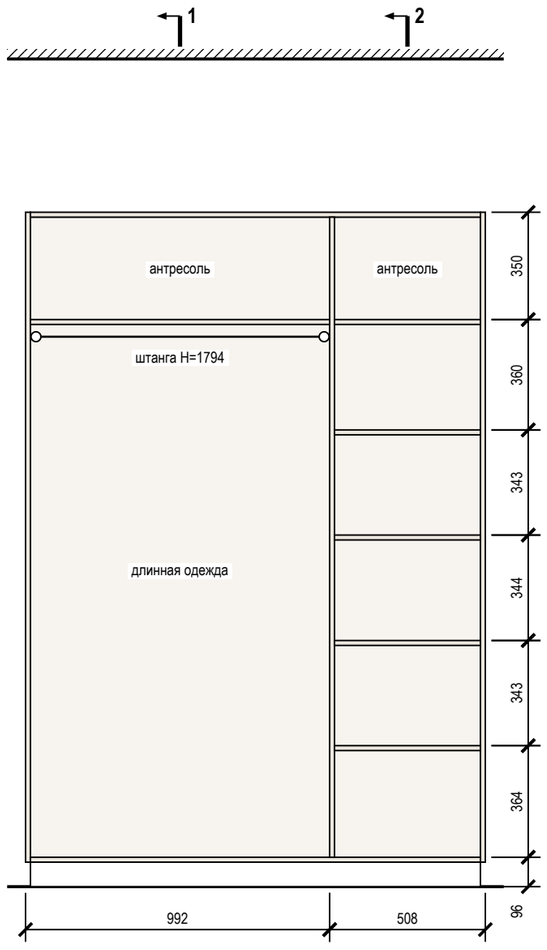

Разрез 1-1

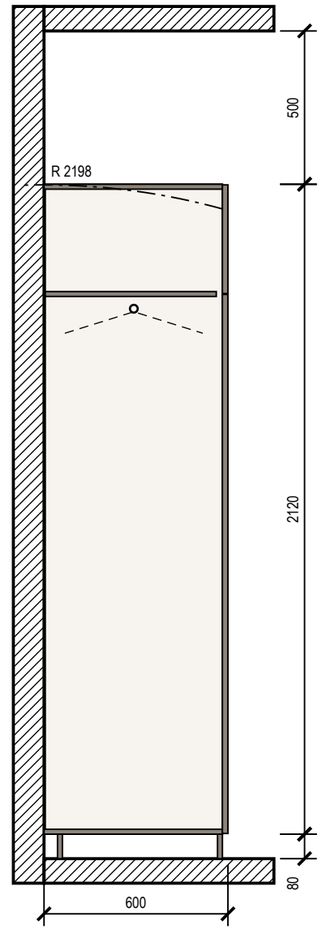

Разрез 2-2

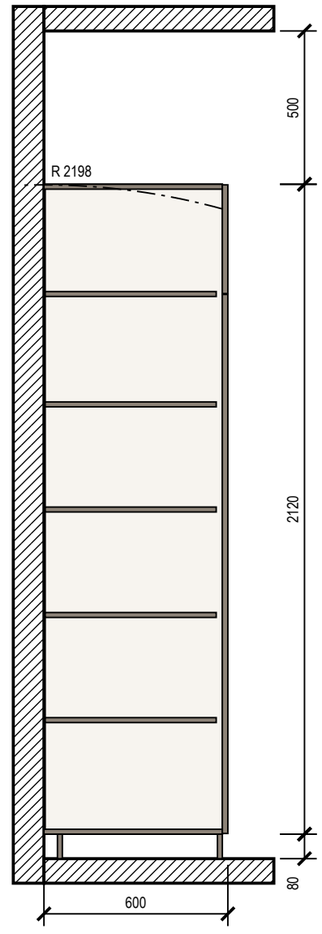

Примечания

1. Размеры — в мм по чистовой отделке; изделие 1500×600×2200 (Ш×Г×В). Перед раскроем — контрольный замер цеха после чистовой отделки стен, пола и потолка.
2. Корпус — ЛДСП 16 мм, задняя стенка ХДФ 4 мм в паз, цоколь 80 мм на регулируемых опорах; фасады накладные — МДФ 18 мм, эмаль матовая, 18 мм; цвет — по колерной карте; петли с доводчиком: фасад 1759 мм — 4 петли, фасад 355 мм — 2 петли.
3. Кромка: скрытые торцы 0,4 мм, видимые 2 мм (ПВХ/АБС).
4. Номинальные зазоры: между фасадами 3 мм, фасад — стена и фасад — потолок не менее 3 мм, фасад ящика — стойка 2 мм.
5. Присадка по 32-й системе — выполняет цех.
6. Зазор до потолка 500 мм.
7. Подъём корпуса: диагональ боковины без цоколя $\sqrt{(2120^2 + 582^2)} = 2198$ мм < 2700 мм до потолка — корпус собирается лёжа, поднимается поворотом и ставится на цоколь.
8. Крепление к стене от опрокидывания — уголки 2 шт. к несущему основанию (монтажная схема шкафов).

Условные обозначения

- фасад распашной: линии сходятся к стороне петель
- корпус и полки ЛДСП (вид на стену)
- задняя стенка ХДФ
- деталь в разрезе
- штанга для плечиков (на разрезе — плечики 450 мм)
- траектория угла корпуса при подъёме в проектное положение

Допущения и предложения на листе

Основа листа: взаимное расположение помещений, контур дома 9600 × 8000 и раскладка этажей подобраны проектировщиком под габариты помещений брифа; обмер и проект АР — задание (К-1); высота потолка 2900 мм — по брифу, не замерена; перекрытие 330 мм и отметка 2-го этажа +3,230 приняты; проект КР — задание (К-2); наружные стены 400 мм, перегородки 120 мм приняты (в брифе толщин нет) (К-1); разрешённая мощность 15 кВт принята по типовым ТУ для частного дома (К-4); подрайон климата не задан — принят не северный (жилые от 2,5 м) (К-7).

Знак «*» — принято, не замерено и не подтверждено (замерить на объекте): К-2: отметка чистого пола этажа «2-й этаж» +3,230 — отметка чистого пола 2-го этажа +3,230 принята: высота потолка 2900 по брифу + перекрытие с полом 330 (конструкция перекрытия не задана; проект КР — задание).

См. лист открытых вопросов (лист 7, записи К-1, К-2, К-4; лист 8, запись К-7).

1000 мм · печать 1:1

Изм.	Кол.уч	Лист	№ док.	Подп.	Дата
Разраб.		Кырлан А.С.			04.11.26
Пров.					
ГИП					
Н. контр.					
Утв.					

ГД-2026-012-АИ

Дом 120 м²

Общая площадь 147,36* м² · * размеры приняты, не замерены (реестр — л. 7–9, К-1)

Дизайн-проект интерьера

Стадия	Лист	Листов
РП	100	175

Шкаф распашной Дт3

М 1:20

Кырлан Александр Сергеевич


выпуск 04.11.2026 № 4dfa962484 · стр. 103 из 180

Система хранения Гд1


Гардеробная (пом. 8) · вид из помещения · размеры в мм, отметки в м от ±0,000 (чистый пол 1-го этажа)

ПРЕДВАРИТЕЛЬНО · не для производства работ · открыто пунктов: 11 (реестр — л. 7–9)


Общий вид

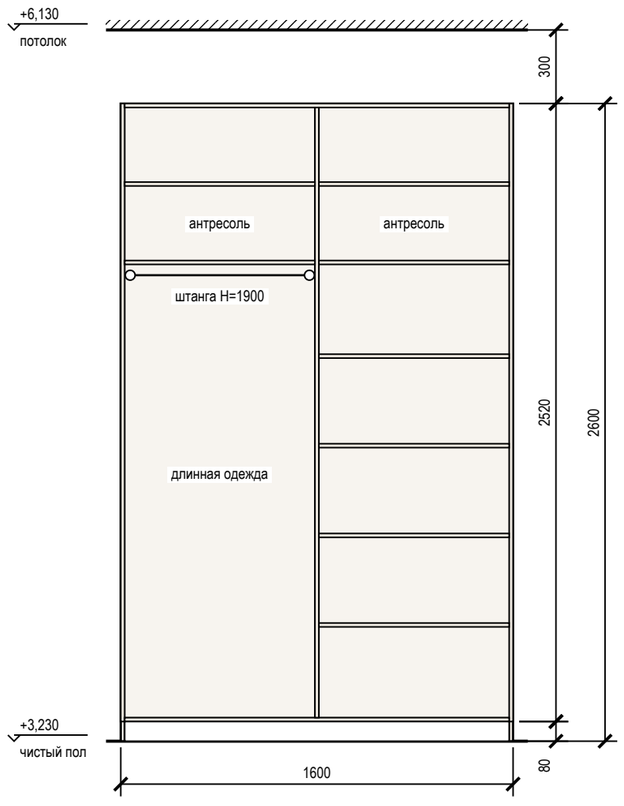


Наполнение, размеры в свету

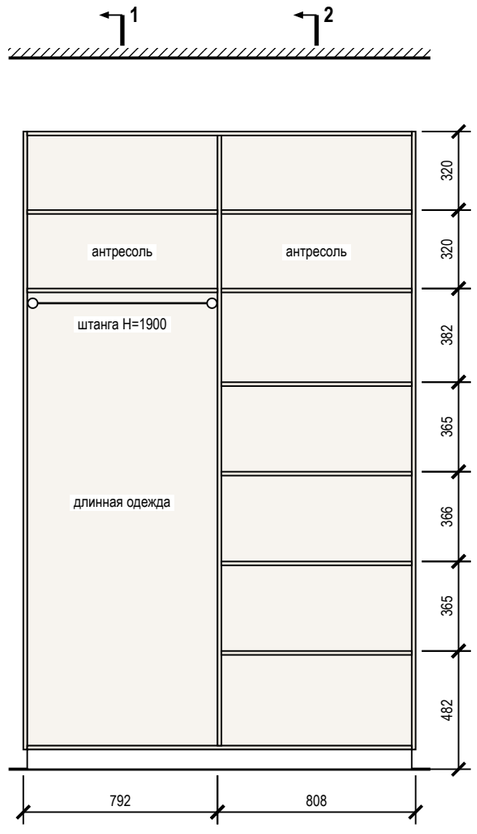

Разрез 1-1

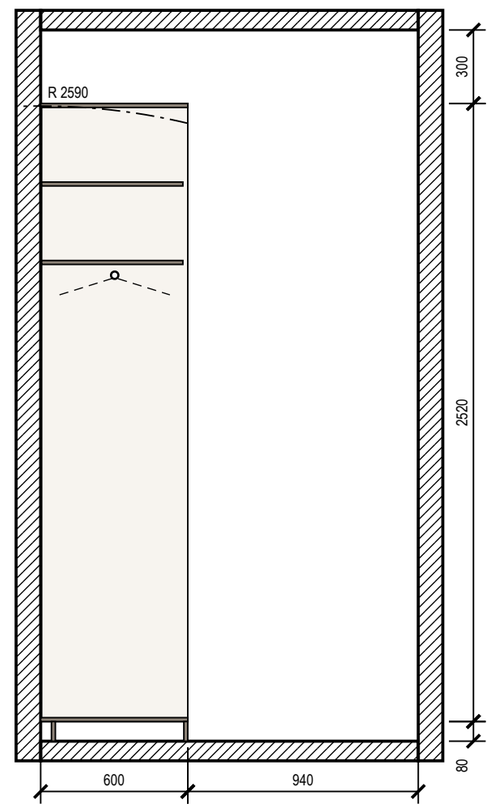

Разрез 2-2

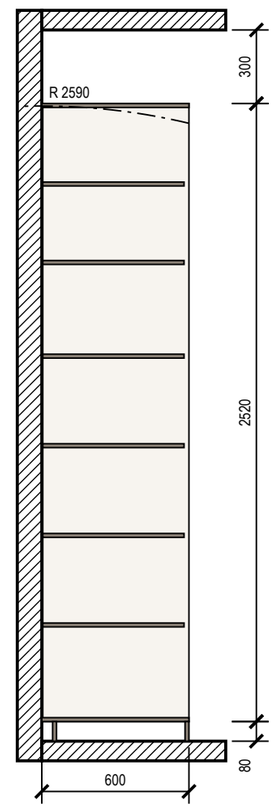

Примечания

1. Размеры — в мм по чистовой отделке; изделие 1600×600×2600 (Ш×Г×В). Перед раскроем — контрольный замер цеха после чистовой отделки стен, пола и потолка.
2. Корпус — ЛДСП 16 мм, задняя стенка ХДФ 4 мм в паз, цоколь 80 мм на регулируемых опорах; открытая система: без фасадов.
3. Кромка: скрытые торцы 0,4 мм, видимые 2 мм (ПВХ/АБС).
4. Присадка по 32-й системе — выполняет цех.
5. Зазор до потолка 300 мм.
6. Подъём корпуса: диагональ боковины без цоколя √(2520² + 600²) = 2590 мм < 2900 мм до потолка — корпус собирается лёжа, поднимается поворотом и ставится на цоколь.
7. Крепление к стене от опрокидывания — уголки 2 шт. к несущему основанию (монтажная схема шкафов).
8. Проход перед изделием 940 мм показан на разрезе 1-1.

Условные обозначения

- корпус и полки ЛДСП (вид на стену)
- задняя стенка ХДФ
- деталь в разрезе
- штанга для плечиков (на разрезе — плечики 450 мм)
- траектория угла корпуса при подъёме в проектное положение

Допущения и предложения на листе

Основа листа: взаимное расположение помещений, контур дома 9600 × 8000 и раскладка этажей подобраны проектировщиком под габариты помещений брифа; обмер и проект АР — задание (К-1); высота потолка 2900 мм — по брифу, не замерена; перекрытие 330 мм и отметка 2-го этажа +3,230 приняты; проект КР — задание (К-2); наружные стены 400 мм, перегородки 120 мм приняты (в брифе толщин нет) (К-1); разрешённая мощность 15 кВт принята по типовым ТУ для частного дома (К-4); подрайон климата не задан — принят не северный (жилые от 2,5 м) (К-7).

Знак «*» — принято, не замерено и не подтверждено (замерить на объекте): К-2: отметка чистого пола этажа «2-й этаж» +3,230 — отметка чистого пола 2-го этажа +3,230 принята: высота потолка 2900 по брифу + перекрытие с полом 330 (конструкция перекрытия не задана; проект КР — задание).

См. лист открытых вопросов (лист 7, записи К-1, К-2, К-4; лист 8, запись К-7).

1000 мм · печать 1:1

Изм.	Кол.уч	Лист	№ док.	Подп.	Дата
Разраб.		Кырлан А.С.			04.11.26
Пров.					
ГИП					
Н. контр.					
Утв.					

ГД-2026-012-АИ

Дом 120 м²

Общая площадь 147,36* м² · * размеры приняты, не замерены (реестр — л. 7–9, К-1)

Дизайн-проект интерьера

Стадия	Лист	Листов
РП	101	175

Система хранения Гд1

М 1:25

Кырлан Александр Сергеевич


выпуск 04.11.2026 № 4dfa962484 · стр. 104 из 180

Система хранения Гд2


Гардеробная (пом. 8) · вид из помещения · размеры в мм, отметки в м от ±0,000 (чистый пол 1-го этажа)

ПРЕДВАРИТЕЛЬНО · не для производства работ · открыто пунктов: 11 (реестр — л. 7–9)


Общий вид

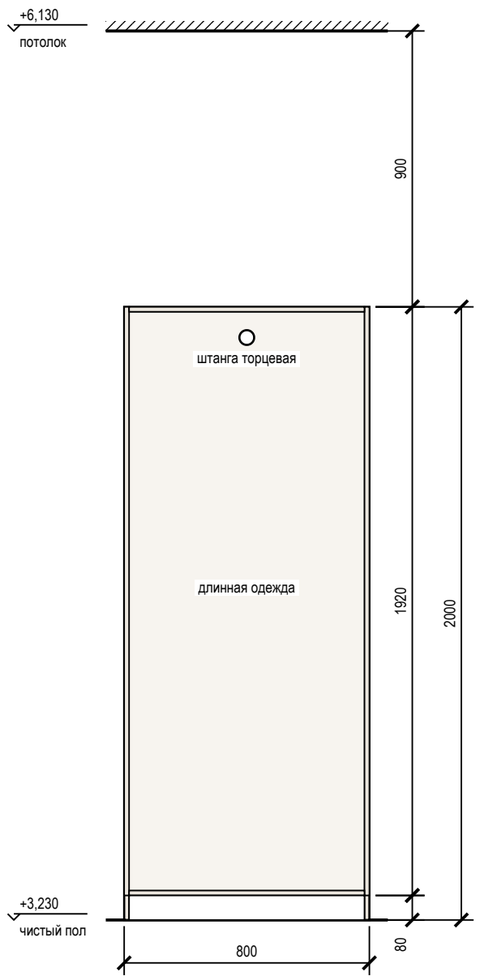

Наполнение, размеры в свету

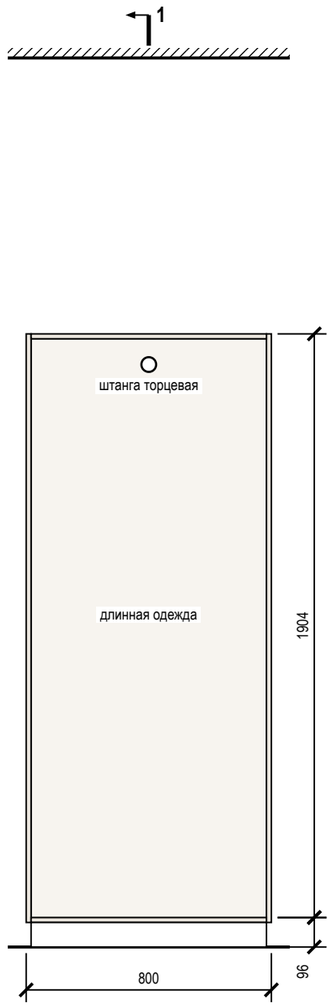

Разрез 1-1

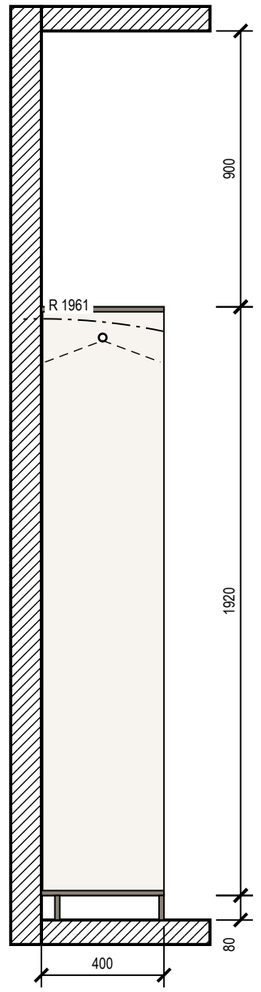

Примечания

1. Размеры — в мм по чистовой отделке; изделие 800×400×2000 (Ш×Г×В). Перед раскроем — контрольный замер цеха после чистовой отделки стен, пола и потолка.
2. Корпус — ЛДСП 16 мм, задняя стенка ХДФ 4 мм в паз, цоколь 80 мм на регулируемых опорах; открытая система: без фасадов.
3. Кромка: скрытые торцы 0,4 мм, видимые 2 мм (ПВХ/АБС).
4. Присадка по 32-й системе — выполняет цех.
5. Зазор до потолка 900 мм.
6. Подъём корпуса: диагональ боковины без цоколя √(1920² + 400²) = 1961 мм < 2900 мм до потолка — корпус собирается лёжа, поднимается поворотом и ставится на цоколь.
7. Крепление к стене от опрокидывания — уголки 2 шт. к несущему основанию (монтажная схема шкафов).

Условные обозначения

- корпус и полки ЛДСП (вид на стену)
- задняя стенка ХДФ
- деталь в разрезе
- штанга для плечиков (на разрезе — плечики 450 мм)
- траектория угла корпуса при подъёме в проектное положение

Допущения и предложения на листе

Основа листа: взаимное расположение помещений, контур дома 9600 × 8000 и раскладка этажей подобраны проектировщиком под габариты помещений брифа; обмер и проект АР — задание (К-1); высота потолка 2900 мм — по брифу, не замерена; перекрытие 330 мм и отметка 2-го этажа +3,230 приняты; проект КР — задание (К-2); наружные стены 400 мм, перегородки 120 мм приняты (в брифе толщин нет) (К-1); разрешённая мощность 15 кВт принята по типовым ТУ для частного дома (К-4); подрайон климата не задан — принят не северный (жилые от 2,5 м) (К-7).

Знак «*» — принято, не замерено и не подтверждено (замерить на объекте): К-2: отметка чистого пола этажа «2-й этаж» +3,230 — отметка чистого пола 2-го этажа +3,230 принята: высота потолка 2900 по брифу + перекрытие с полом 330 (конструкция перекрытия не задана; проект КР — задание).

См. лист открытых вопросов (лист 7, записи К-1, К-2, К-4; лист 8, запись К-7).

1000 мм · печать 1:1

Изм.	Кол.уч	Лист	№ док.	Подп.	Дата
Разраб.		Кырлан А.С.			04.11.26
Пров.					
ГИП					
Н. контр.					
Утв.					

ГД-2026-012-АИ

Дом 120 м²

Общая площадь 147,36* м² · * размеры приняты, не замерены (реестр — л. 7–9, К-1)

Дизайн-проект интерьера

Стадия	Лист	Листов
РП	102	175

Система хранения Гд2

М 1:20

Кырлан Александр Сергеевич


выпуск 04.11.2026 № 4dfa962484 · стр. 105 из 180

Система хранения Кл1


Кладовая (пом. 9) · вид из помещения · размеры в мм, отметки в м от ±0,000 (чистый пол 1-го этажа)

ПРЕДВАРИТЕЛЬНО · не для производства работ · открыто пунктов: 11 (реестр — л. 7–9)


Общий вид

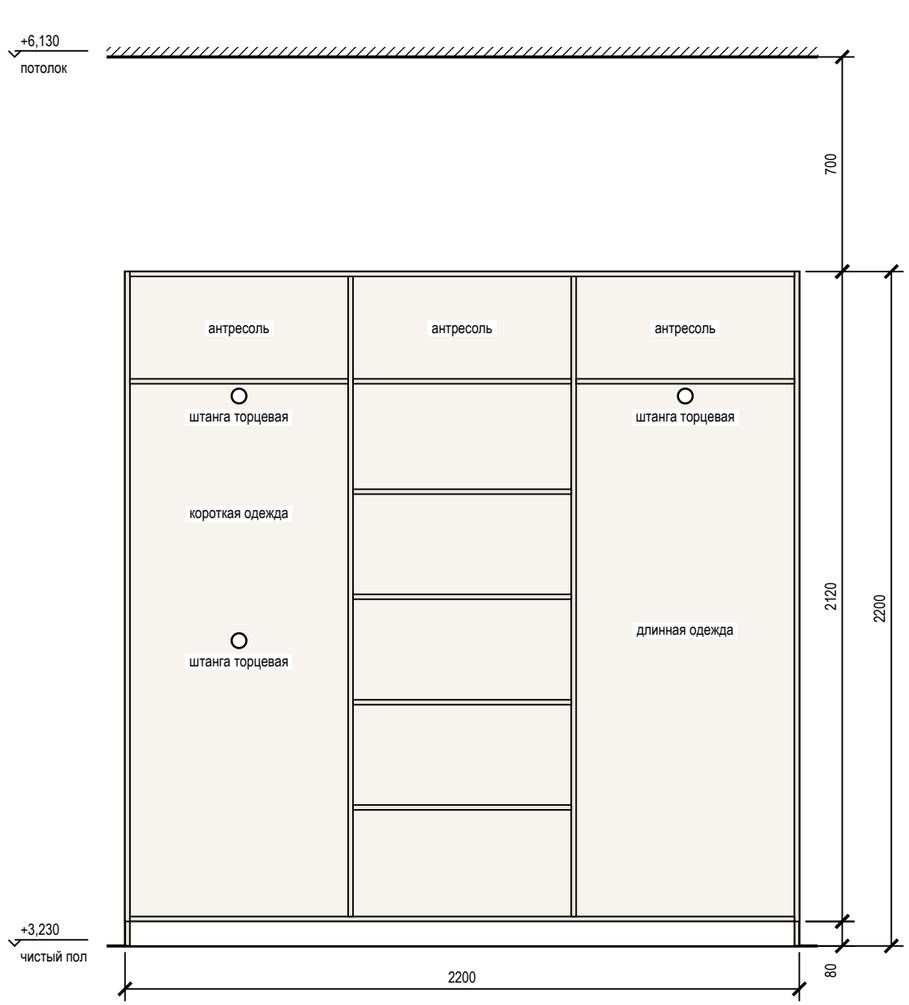


Наполнение, размеры в свету

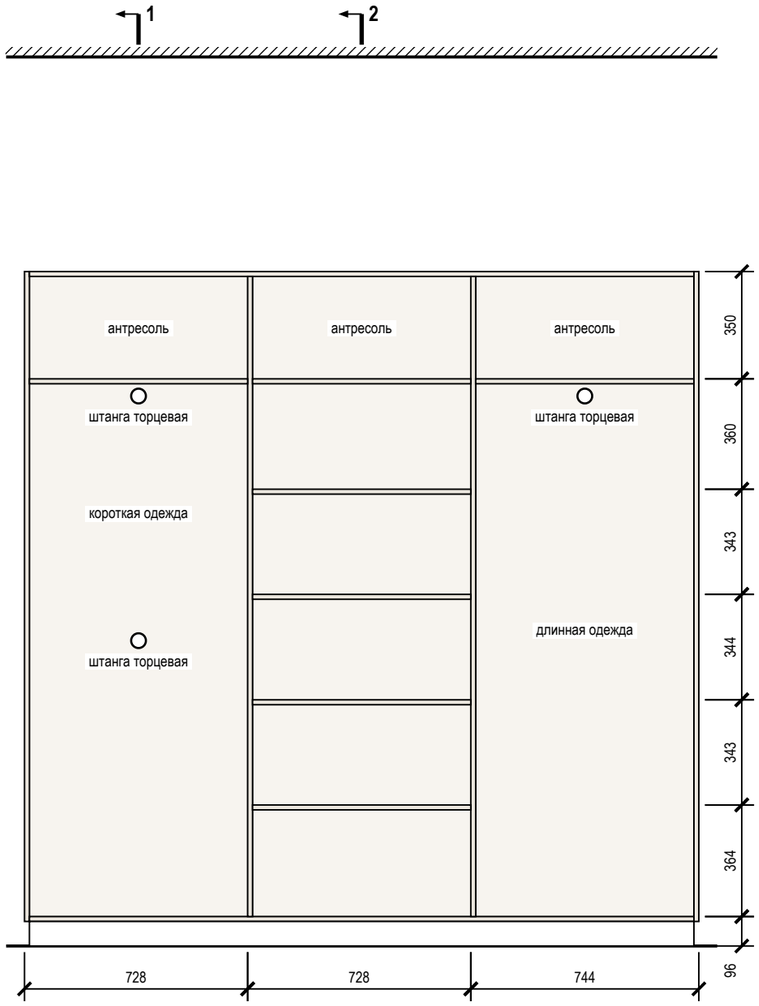

Разрез 1-1

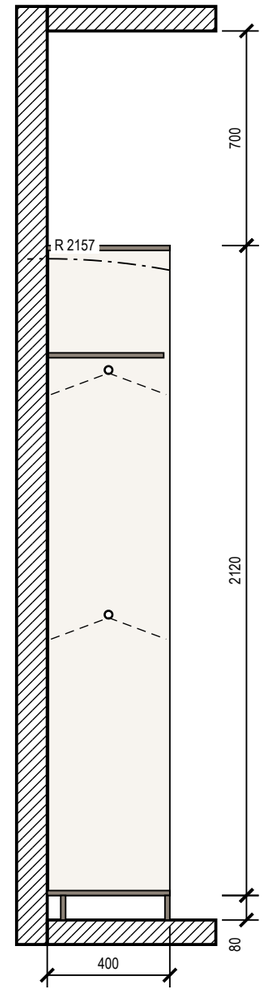

Разрез 2-2

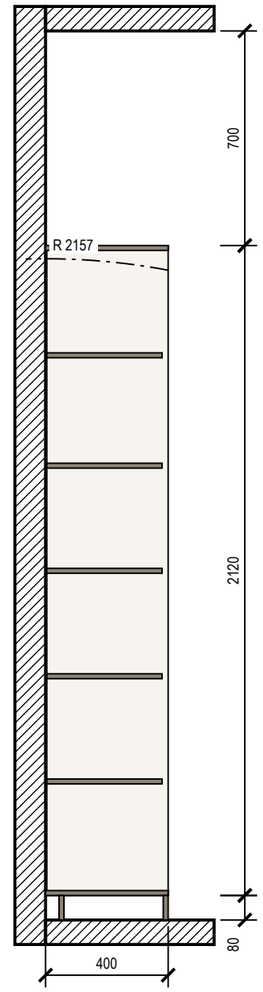

Примечания

1. Размеры — в мм по чистовой отделке; изделие 2200×400×2200 (Ш×Г×В). Перед раскроем — контрольный замер цеха после чистовой отделки стен, пола и потолка.
2. Корпус — ЛДСП 16 мм, задняя стенка ХДФ 4 мм в паз, цоколь 80 мм на регулируемых опорах; открытая система: без фасадов.
3. Кромка: скрытые торцы 0,4 мм, видимые 2 мм (ПВХ/АБС).
4. Присадка по 32-й системе — выполняет цех.
5. Зазор до потолка 700 мм.
6. Подъём корпуса: диагональ боковины без цоколя √(2120² + 400²) = 2157 мм < 2900 мм до потолка — корпус собирается лёжа, поднимается поворотом и ставится на цоколь.
7. Крепление к стене от опрокидывания — уголки 2 шт. к несущему основанию (монтажная схема шкафов).

Условные обозначения

- корпус и полки ЛДСП (вид на стену)
- задняя стенка ХДФ
- деталь в разрезе
- штанга для плечиков (на разрезе — плечики 450 мм)
- траектория угла корпуса при подъёме в проектное положение

Допущения и предложения на листе

Основа листа: взаимное расположение помещений, контур дома 9600 × 8000 и раскладка этажей подобраны проектировщиком под габариты помещений брифа; обмер и проект АР — задание (К-1); высота потолка 2900 мм — по брифу, не замерена; перекрытие 330 мм и отметка 2-го этажа +3,230 приняты; проект КР — задание (К-2); наружные стены 400 мм, перегородки 120 мм приняты (в брифе толщин нет) (К-1); разрешённая мощность 15 кВт принята по типовым ТУ для частного дома (К-4); подрайон климата не задан — принят не северный (жилые от 2,5 м) (К-7).

Знак «*» — принято, не замерено и не подтверждено (замерить на объекте): К-2: отметка чистого пола этажа «2-й этаж» +3,230 — отметка чистого пола 2-го этажа +3,230 принята: высота потолка 2900 по брифу + перекрытие с полом 330 (конструкция перекрытия не задана; проект КР — задание).

См. лист открытых вопросов (лист 7, записи К-1, К-2, К-4; лист 8, запись К-7).

1000 мм · печать 1:1

Изм.	Кол.уч	Лист	№ док.	Подп.	Дата
Разраб.		Кырлан А.С.			04.11.26
Пров.					
ГИП					
Н. контр.					
Утв.					

ГД-2026-012-АИ

Дом 120 м²

Общая площадь 147,36* м² · * размеры приняты, не замерены (реестр — л. 7–9, К-1)

Дизайн-проект интерьера

Стадия	Лист	Листов
РП	103	175

Система хранения Кл1

М 1:20

Кырлан Александр Сергеевич


выпуск 04.11.2026 № 4dfa962484 · стр. 106 из 180

Система хранения Кл2


Кладовая (пом. 9) · вид из помещения · размеры в мм, отметки в м от ±0,000 (чистый пол 1-го этажа)

ПРЕДВАРИТЕЛЬНО · не для производства работ · открыто пунктов: 11 (реестр — л. 7–9)


Общий вид

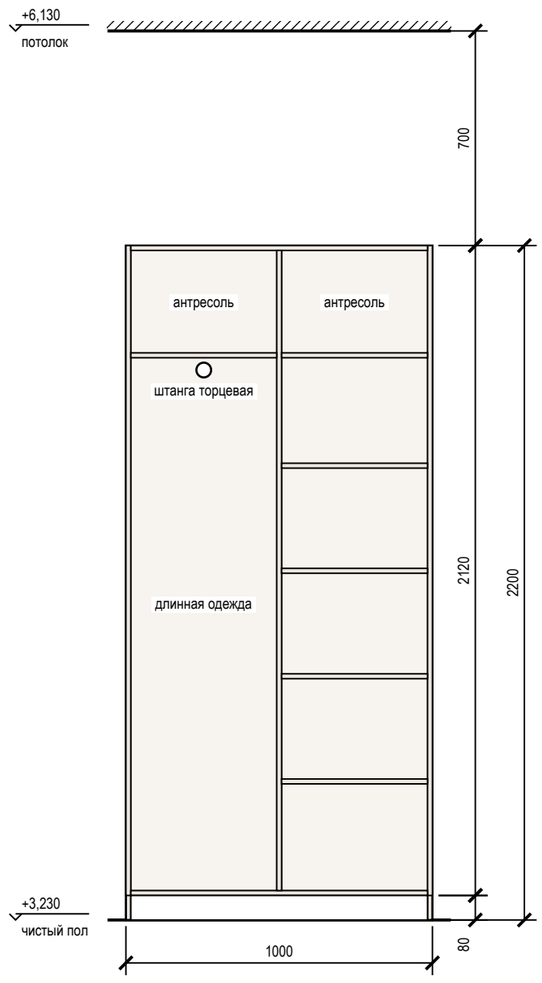


Наполнение, размеры в свету

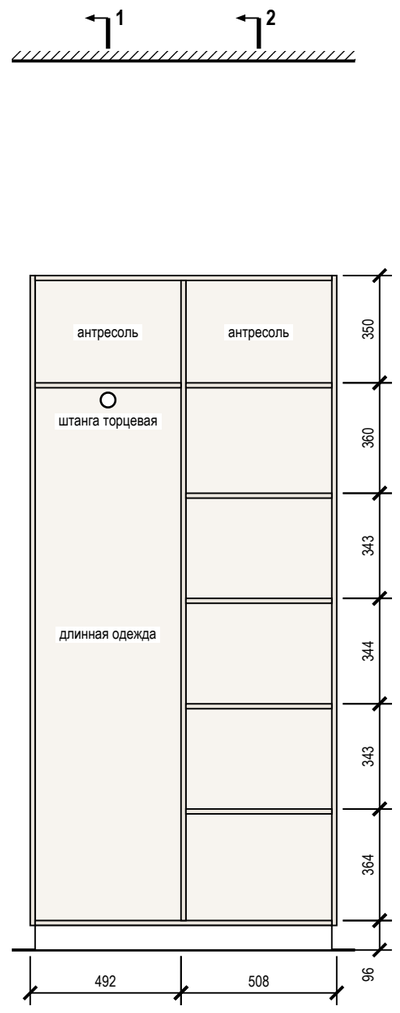

Разрез 1-1

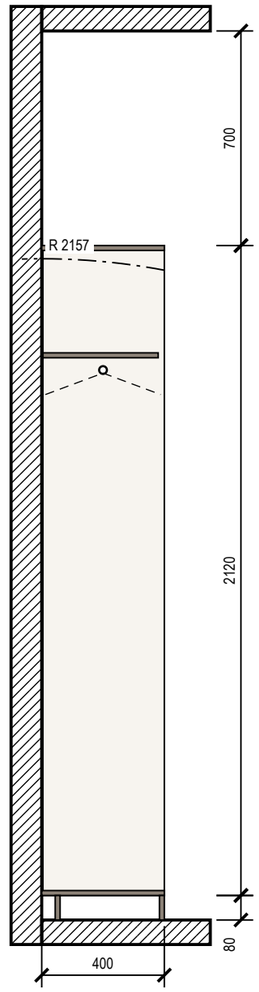

Разрез 2-2

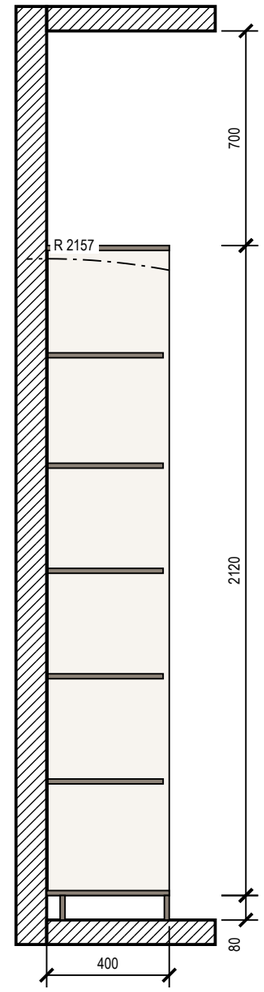

Примечания

1. Размеры — в мм по чистовой отделке; изделие 1000×400×2200 (Ш×Г×В). Перед раскроем — контрольный замер цеха после чистовой отделки стен, пола и потолка.
2. Корпус — ЛДСП 16 мм, задняя стенка ХДФ 4 мм в паз, цоколь 80 мм на регулируемых опорах; открытая система: без фасадов.
3. Кромка: скрытые торцы 0,4 мм, видимые 2 мм (ПВХ/АБС).
4. Присадка по 32-й системе — выполняет цех.
5. Зазор до потолка 700 мм.
6. Подъём корпуса: диагональ боковины без цоколя $\sqrt{(2120^2 + 400^2)} = 2157$ мм < 2900 мм до потолка — корпус собирается лёжа, поднимается поворотом и ставится на цоколь.
7. Крепление к стене от опрокидывания — уголки 2 шт. к несущему основанию (монтажная схема шкафов).

Условные обозначения

- корпус и полки ЛДСП (вид на стену)
- задняя стенка ХДФ
- деталь в разрезе
- штанга для плечиков (на разрезе — плечики 450 мм)
- траектория угла корпуса при подъёме в проектное положение

Допущения и предложения на листе

Основа листа: взаимное расположение помещений, контур дома 9600 × 8000 и раскладка этажей подобраны проектировщиком под габариты помещений брифа; обмер и проект АР — задание (К-1); высота потолка 2900 мм — по брифу, не замерена; перекрытие 330 мм и отметка 2-го этажа +3,230 приняты; проект КР — задание (К-2); наружные стены 400 мм, перегородки 120 мм приняты (в брифе толщин нет) (К-1); разрешённая мощность 15 кВт принята по типовым ТУ для частного дома (К-4); подрайон климата не задан — принят не северный (жилые от 2,5 м) (К-7).

Знак «*» — принято, не замерено и не подтверждено (замерить на объекте): К-2: отметка чистого пола этажа «2-й этаж» +3,230 — отметка чистого пола 2-го этажа +3,230 принята: высота потолка 2900 по брифу + перекрытие с полом 330 (конструкция перекрытия не задана; проект КР — задание).

См. лист открытых вопросов (лист 7, записи К-1, К-2, К-4; лист 8, запись К-7).

1000 мм · печать 1:1

Изм.	Кол.уч	Лист	№ док.	Подп.	Дата
Разраб.		Кырлан А.С.			04.11.26
Пров.					
ГИП					
Н. контр.					
Утв.					

ГД-2026-012-АИ

Дом 120 м²

Общая площадь 147,36* м² · * размеры приняты, не замерены (реестр — л. 7–9, К-1)

Дизайн-проект интерьера

Стадия	Лист	Листов
РП	104	175

Система хранения Кл2

М 1:20

Кырлан Александр Сергеевич


выпуск 04.11.2026 № 4dfa962484 · стр. 107 из 180

Шкаф распашной Дт8


Детская вторая (пом. 12) · вид из помещения · размеры в мм, отметки в м от ±0,000 (чистый пол 1-го этажа)

ПРЕДВАРИТЕЛЬНО · не для производства работ · открыто пунктов: 11 (реестр — л. 7–9)


Вид с фасадами

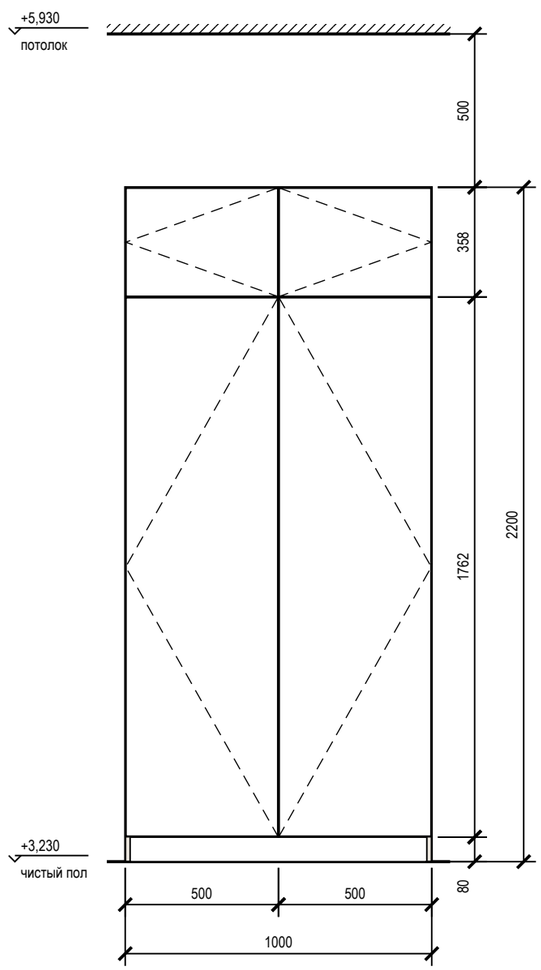

Вид без фасадов

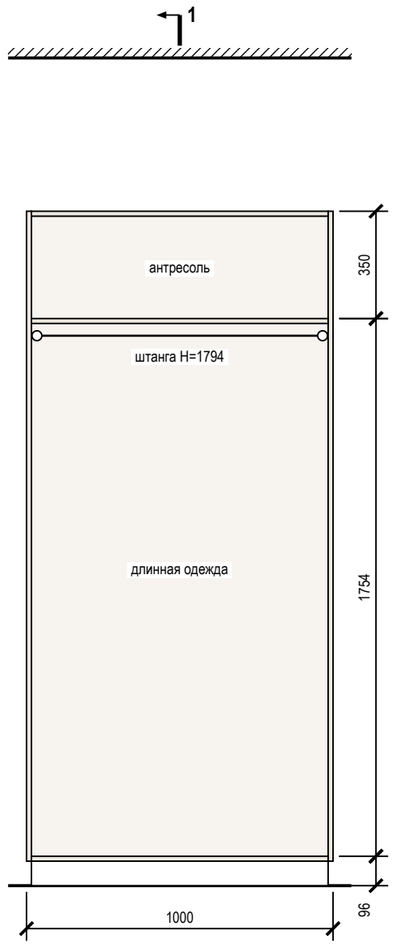

Разрез 1-1

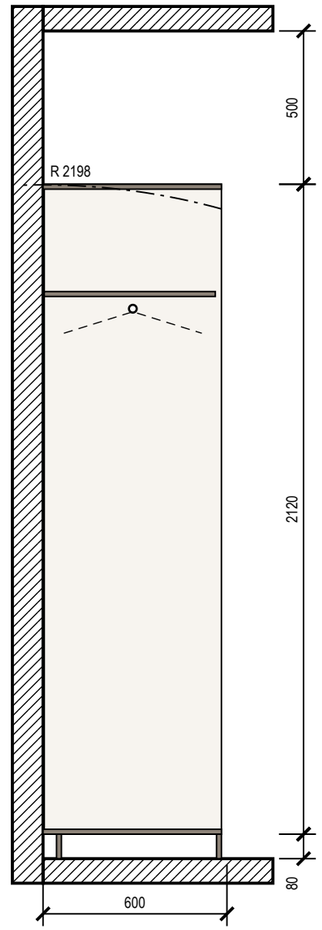

Примечания

1. Размеры — в мм по чистовой отделке; изделие 1000×600×2200 (Ш×Г×В). Перед раскроем — контрольный замер цеха после чистовой отделки стен, пола и потолка.
2. Корпус — ЛДСП 16 мм, задняя стенка ХДФ 4 мм в паз, цоколь 80 мм на регулируемых опорах; фасады накладные — МДФ 18 мм, эмаль матовая, 18 мм; цвет — по колерной карте; петли с доводчиком: фасад 1759 мм — 4 петли, фасад 355 мм — 2 петли.
3. Кромка: скрытые торцы 0,4 мм, видимые 2 мм (ПВХ/АБС).
4. Номинальные зазоры: между фасадами 3 мм, фасад — стена и фасад — потолок не менее 3 мм, фасад ящика — стойка 2 мм.
5. Присадка по 32-й системе — выполняет цех.
6. Зазор до потолка 500 мм.
7. Подъём корпуса: диагональ боковины без цоколя √(2120² + 582²) = 2198 мм < 2700 мм до потолка — корпус собирается лёжа, поднимается поворотом и ставится на цоколь.
8. Крепление к стене от опрокидывания — уголки 2 шт. к несущему основанию (монтажная схема шкафов).

Условные обозначения

- фасад распашной: линии сходятся к стороне петель
- корпус и полки ЛДСП (вид на стену)
- задняя стенка ХДФ
- деталь в разрезе
- штанга для плечиков (на разрезе — плечики 450 мм)
- траектория угла корпуса при подъёме в проектное положение

Допущения и предложения на листе

Основа листа: взаимное расположение помещений, контур дома 9600 × 8000 и раскладка этажей подобраны проектировщиком под габариты помещений брифа; обмер и проект АР — задание (К-1); высота потолка 2900 мм — по брифу, не замерена; перекрытие 330 мм и отметка 2-го этажа +3,230 приняты; проект КР — задание (К-2); наружные стены 400 мм, перегородки 120 мм приняты (в брифе толщин нет) (К-1); разрешённая мощность 15 кВт принята по типовым ТУ для частного дома (К-4); подрайон климата не задан — принят не северный (жилые от 2,5 м) (К-7).

Знак «*» — принято, не замерено и не подтверждено (замерить на объекте): К-2: отметка чистого пола этажа «2-й этаж» +3,230 — отметка чистого пола 2-го этажа +3,230 принята: высота потолка 2900 по брифу + перекрытие с полом 330 (конструкция перекрытия не задана; проект КР — задание).

См. лист открытых вопросов (лист 7, записи К-1, К-2, К-4; лист 8, запись К-7).

1000 мм · печать 1:1

Изм.	Кол.уч	Лист	№ док.	Подп.	Дата
Разраб.		Кырлан А.С.			04.11.26
Пров.					
ГИП					
Н. контр.					
Утв.					

ГД-2026-012-АИ

Дом 120 м²

Общая площадь 147,36* м² · * размеры приняты, не замерены (реестр — л. 7–9, К-1)

Дизайн-проект интерьера

Стадия	Лист	Листов
РП	105	175

Шкаф распашной Дт8

М 1:20

Кырлан Александр Сергеевич


выпуск 04.11.2026 № 4dfa962484 · стр. 108 из 180

Система хранения Дт10


Детская вторая (пом. 12) · вид из помещения · размеры в мм, отметки в м от ±0,000 (чистый пол 1-го этажа)

ПРЕДВАРИТЕЛЬНО · не для производства работ · открыто пунктов: 11 (реестр — л. 7–9)


Общий вид

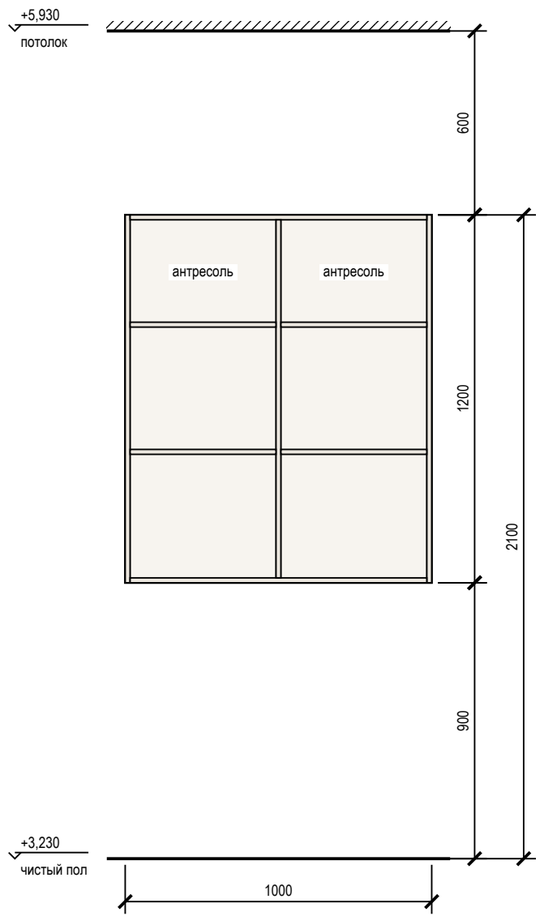

Наполнение, размеры в свету

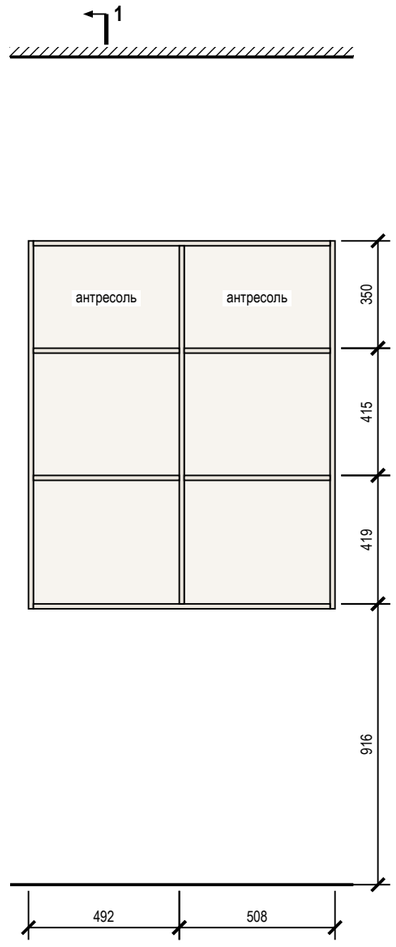

Разрез 1-1

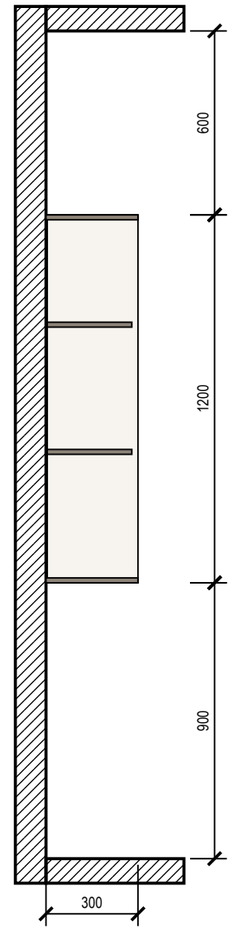

Примечания

1. Размеры — в мм по чистовой отделке; изделие 1000×300×1200 (Ш×Г×В). Перед раскроем — контрольный замер цеха после чистовой отделки стен, пола и потолка.
2. Корпус — ЛДСП 16 мм, задняя стенка ХДФ 4 мм в паз, навесной корпус без цоколя, низ на 900 мм от чистого пола; открытая система: без фасадов.
3. Кромка: скрытые торцы 0,4 мм, видимые 2 мм (ПВХ/АБС).
4. Присадка по 32-й системе — выполняет цех.
5. Зазор до потолка 600 мм.
6. Навесной корпус — на стене: регулируемые навесы на монтажную шину или анкеры в несущее основание; основание стены и шаг анкеров — монтажная схема шкафов.

Условные обозначения

- корпус и полки ЛДСП (вид на стену)
- задняя стенка ХДФ
- деталь в разрезе
- штанга для плечиков (на разрезе — плечики 450 мм)

Допущения и предложения на листе

Основа листа: взаимное расположение помещений, контур дома 9600 × 8000 и раскладка этажей подобраны проектировщиком под габариты помещений брифа; обмер и проект АР — задание (К-1); высота потолка 2900 мм — по брифу, не замерена; перекрытие 330 мм и отметка 2-го этажа +3,230 приняты; проект КР — задание (К-2); наружные стены 400 мм, перегородки 120 мм приняты (в брифе толщин нет) (К-1); разрешённая мощность 15 кВт принята по типовым ТУ для частного дома (К-4); подрайон климата не задан — принят не северный (жилые от 2,5 м) (К-7).

Знак «*» — принято, не замерено и не подтверждено (замерить на объекте): К-2: отметка чистого пола этажа «2-й этаж» +3,230 — отметка чистого пола 2-го этажа +3,230 принята: высота потолка 2900 по брифу + перекрытие с полом 330 (конструкция перекрытия не задана; проект КР — задание).

См. лист открытых вопросов (лист 7, записи К-1, К-2, К-4; лист 8, запись К-7).

1000 мм · печать 1:1

Изм.	Кол.уч	Лист	№ док.	Подп.	Дата
Разраб.		Кырлан А.С.			04.11.26
Пров.					
ГИП					
Н. контр.					
Утв.					

ГД-2026-012-АИ

Дом 120 м²

Общая площадь 147,36* м² · * размеры приняты, не замерены (реестр — л. 7–9, К-1)

Дизайн-проект интерьера	Стадия	Лист	Листов
	РП	106	175
Система хранения Дт10 М 1:20	**Кырлан Александр Сергеевич**		


выпуск 04.11.2026 № 4dfa962484 · стр. 109 из 180

Кухня (пом. 1). Развёртка гарнитура


Гостиная-кухня (пом. 1) · стена А · вид из помещения · размеры в мм, отметки в м от ±0,000 (чистый пол 1-го этажа)

ПРЕДВАРИТЕЛЬНО · не для производства работ · открыто пунктов: 11 (реестр — л. 7–9)


Вид с фасадами

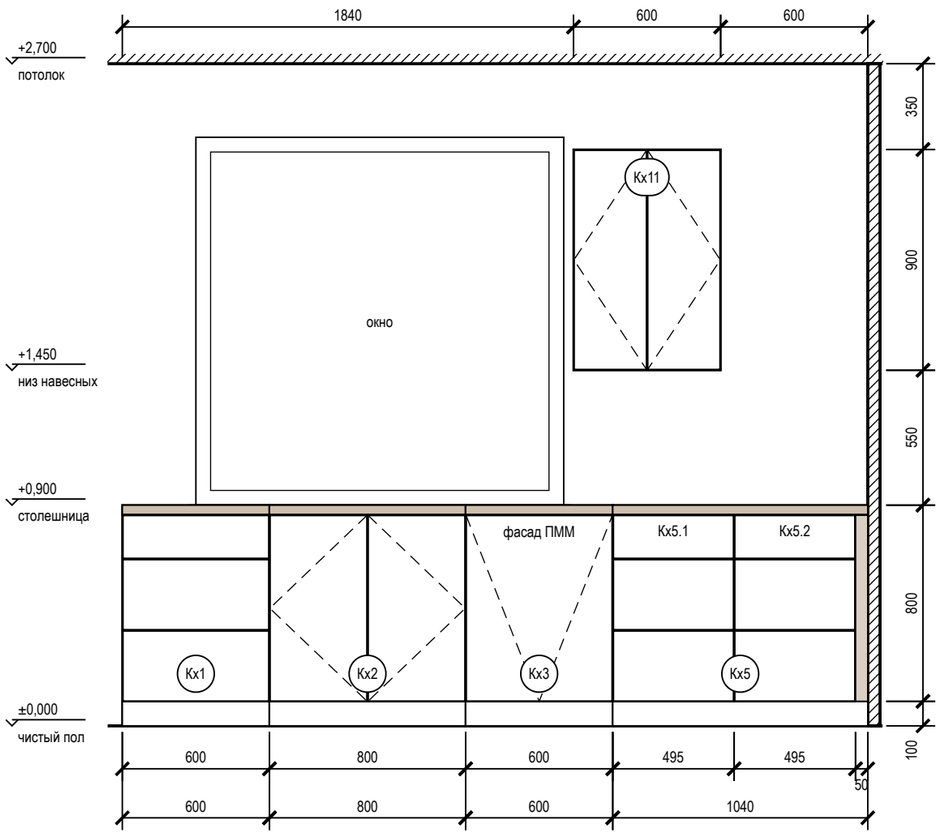

Вид без фасадов (наполнение, выводы)

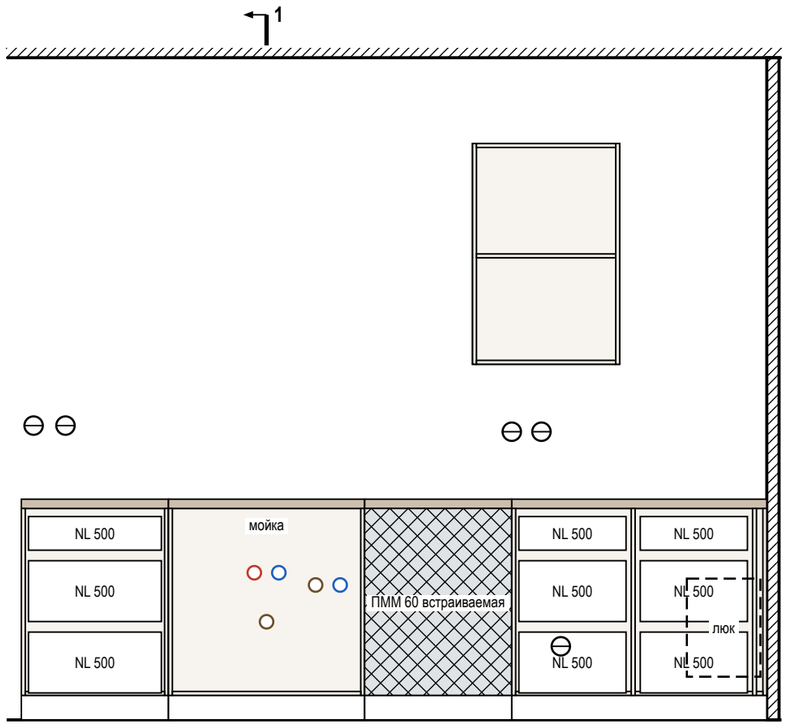

Разрез 1-1

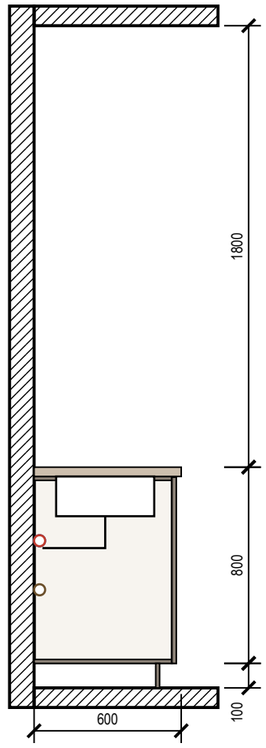

Условные обозначения

- фасад распашной: линии сходятся к стороне петель
- фасад ящика, карго
- встраиваемая техника
- столешница
- доборная планка
- деталь в разрезе
- К1 — марка изделия или модуля (на схеме расположения под ней — лист изделия)
- розетка на стене
- вывод кабеля к технике
- В1 — вывод воды В1 / Т3, канализации К1

Примечания

1. Размеры — в мм по чистовой отделке, вид из помещения; марки — как на плане расстановки. Перед раскроем — контрольный замер цеха после фартука и пола.
2. Корпуса — ЛДСП 16 мм, задняя стенка ХДФ 4 мм; фасады — МДФ, эмаль матовая 18 мм, цвет по колерной карте; столешница 38 мм, свес 20 мм; цоколь 100 мм.
3. Кромка: скрытые торцы 0,4 мм, видимые 2 мм. Номинальные зазоры: между фасадами 3 мм, фасад — столешница 3 мм, фасад — стена не менее 3 мм.
4. Ящики полного выдвижения и петли — с доводчиком; присадка по 32-й системе — выполняет цех.
5. Ниши техники — по монтажным схемам выбранных моделей: решётка в цоколе и канал за пеналом холодильника, зазор за духовым шкафом, фасад ПММ на двери машины.
6. Кх5: сервисный люк к стоякам Ст К1-2 (кухня)*, Ст В1-2*, Ст Т3-2* — съёмная панель 300×400 мм в задней стенке на саморезах (по виду без фасадов, штриховой контур «люк»), доступ через фасад модуля; короб стояков за модулем — с ревизией напротив люка (лист ВК).

Допущения и предложения на листе

Основа листа: взаимное расположение помещений, контур дома 9600 × 8000 и раскладка этажей подобраны проектировщиком под габариты помещений брифа; обмер и проект АР — задание (К-1); высота потолка 2900 мм — по брифу, не замерена; перекрытие 330 мм и отметка 2-го этажа +3,230 приняты; проект КР — задание (К-2); наружные стены 400 мм, перегородки 120 мм приняты (в брифе толщин нет) (К-1); разрешённая мощность 15 кВт принята по типовым ТУ для частного дома (К-4); подрайон климата не задан — принят не северный (жилые от 2,5 м) (К-7).

Знак «*» — принято, не замерено и не подтверждено (замерить на объекте): К-5: Ст К1-2 (кухня), Ст В1-2, Ст Т3-2 — положение стояка принято проектировщиком (проект ВК дома не передан), не замерено.

См. лист открытых вопросов (лист 7, записи К-1, К-2, К-4, К-5; лист 8, запись К-7).

1000 мм · печать 1:1

Изм.	Кол.уч	Лист	№ док.	Подп.	Дата
Разраб.		Кырлан А.С.			04.11.26
Пров.					
ГИП					
Н. контр.					
Утв.					

ГД-2026-012-АИ

Дом 120 м²

Общая площадь 147,36* м² · * размеры приняты, не замерены (реестр — л. 7–9, К-1)

Дизайн-проект интерьера	Стадия	Лист	Листов
	РП	107	175

Кухня (пом. 1). Развёртка гарнитура

М 1:25

Кырлан Александр Сергеевич


выпуск 04.11.2026 № 4dfa962484 · стр. 110 из 180

Кухня (пом. 1). Монтажная схема


Гостиная-кухня (пом. 1) · стена А · размеры в мм от чистых поверхностей, высоты — от чистого пола

ПРЕДВАРИТЕЛЬНО · не для производства работ · открыто пунктов: 11 (реестр — л. 7–9)

Привязка выводов и крепление модулей

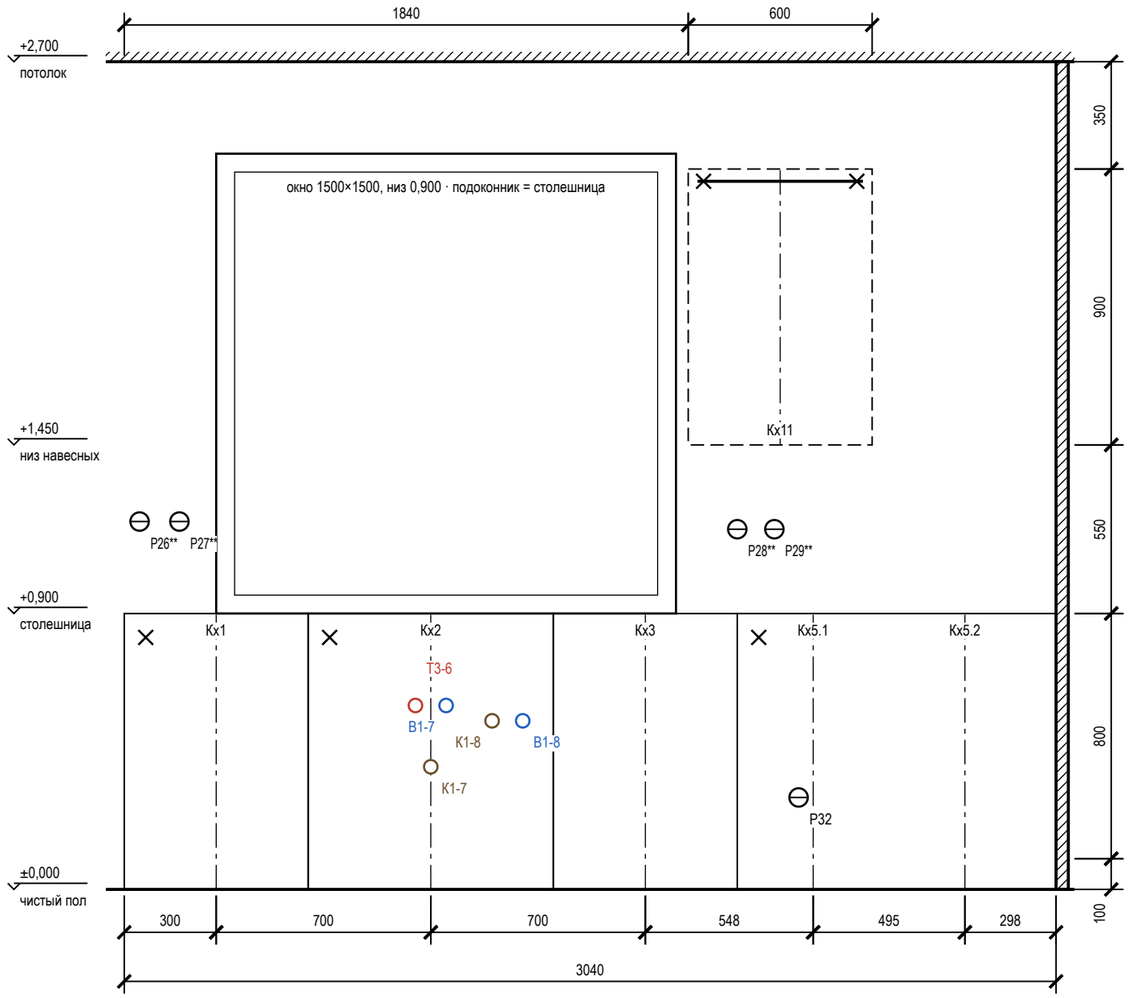

План столешницы

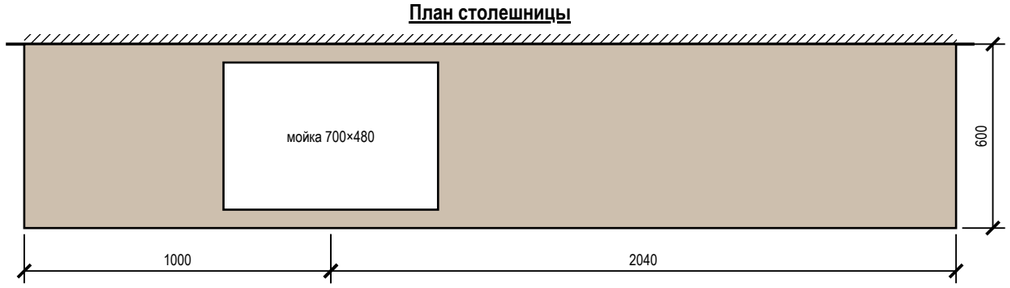

Привязка выводов к осям модулей

Код	Назначение	Модуль	От оси, мм	Н, мм	Размещение
Р26**	розетка ×2 — фартук	Кх1	−250	1200	над столешницей (фартук)
Р27**	розетка — фартук	Кх1	−120	1200	над столешницей (фартук)
Т3-6	Т3 — межос. 100	Кх2	−50	600	в модуле мойки
К1-7	К1 Ø50 — мойка	Кх2	0	400	в модуле мойки
В1-7	В1 — межос. 100	Кх2	+50	600	в модуле мойки
К1-8	К1 Ø40 — слив ПММ в шкафу мойки	Кх2	+200	550	в модуле мойки
В1-8	В1 — кран ПММ в шкафу мойки	Кх2	+300	550	в модуле мойки
Р28**	розетка ×2 — фартук	Кх3	+300	1175	над столешницей (фартук)
Р29**	розетка — фартук	Кх5.1	−126	1175	над столешницей (фартук)
Р32	розетка — посудомоечная машина	Кх5.1	−47	300	в соседнем модуле, за ящиком

Зазоры под отделку

Поверхность	Отделка	Зазор, мм	Учесть
фартук	керамогранит	10	от чернового основания до корпуса навесных и столешницы
стены	окраска	5	под штукатурку и шпаклёвку за пеналом
пол	инженерная доска		цоколь — после укладки пола, опоры ±20 мм

Условные обозначения

- нижний модуль, пенал (контур)
- невидимый контур: навесной модуль, корпус под столешницей
- ось модуля (от неё — привязка вывода)
- анкер / уголок крепления к стене
- розетка на стене
- вывод кабеля к технике
- В1 — вывод воды В1 / Т3, канализации К1

Примечания

1. Окно над Кх1, Кх2, Кх3: низ проёма на 900 мм от пола, столешница на 900 мм, под окном мойка Кх2 — смеситель упирается в створку, открывающуюся внутрь; примыкание столешницы к откосу и подоконнику — до решения: решение по К-8; столешницу у окна не раскраивать до решения.
2. Выводы — по проекту электрики и ВК; привязка по горизонтали — от оси модуля (плюс — вправо по виду), по высоте — от чистого пола до оси вывода.
3. Пенал — уголки к стене 2 шт. сверху; нижние модули — стяжками между собой и уголком к стене; ряд выставить по уровню опорами цоколя.
4. Розетки над столешницей — не ниже 150 мм над ней и не за корпусом техники; розетка за ПММ, духовым шкафом и холодильником — только в соседнем модуле или в зоне цоколя с доступом.
5. Столешница — вырезы по шаблонам выбранных моделей мойки и варочной панели; торцы у стены — герметик, пристеночный плинтус.

1000 мм · печать 1:1

Допущения и предложения на листе

Основа листа: взаимное расположение помещений, контур дома 9600 × 8000 и раскладка этажей подобраны проектировщиком под габариты помещений брифа; обмер и проект АР — задание (К-1); высота потолка 2900 мм — по брифу, не замерена; перекрытие 330 мм и отметка 2-го этажа +3,230 приняты; проект КР — задание (К-2); наружные стены 400 мм, перегородки 120 мм приняты (в брифе толщин нет) (К-1); разрешённая мощность 15 кВт принята по типовым ТУ для частного дома (К-4); подрайон климата не задан — принят не северный (жилые от 2,5 м) (К-7).
Знак «**» — предложение проектировщика, заказчиком не утверждено (согласовать с заказчиком): Р26, Р27 — Сдвиг под раскладку плитки фартука (стена А) на 100 мм выше — ось на шве или в центре плитки, привязка по таблице листа; Р28 — Сдвиг под раскладку плитки фартука (стена А) на 75 мм выше — ось на шве или в центре плитки, привязка по таблице листа; Р29 — Сдвиг под раскладку плитки фартука (стена А) на 29 мм вдоль стены и на 75 мм выше — ось на шве или в центре плитки, привязка по таблице листа.
Открытые вопросы и конфликты по листу: К-8.
См. лист открытых вопросов (лист 7, записи К-1, К-2, К-4; лист 8, записи К-7, К-8).

Изм.	Кол.уч	Лист	№ док.	Подп.	Дата
Разраб.		Кырлан А.С.			04.11.26
Пров.					
ГИП					
Н. контр.					
Утв.					

ГД-2026-012-АИ

Дом 120 м²

Общая площадь 147,36* м² · * размеры приняты, не замерены (реестр — л. 7–9, К-1)

Дизайн-проект интерьера

Стадия	Лист	Листов
РП	108	175

Кухня (пом. 1). Монтажная схема

М 1:20


Кырлан Александр Сергеевич

выпуск 04.11.2026 № 4dfa962484 · стр. 111 из 180


Кухня (пом. 1). Развёртка гарнитура

Гостиная-кухня (пом. 1) · стена Б · вид из помещения · размеры в мм, отметки в м от ±0,000 (чистый пол 1-го этажа)


Вид с фасадами

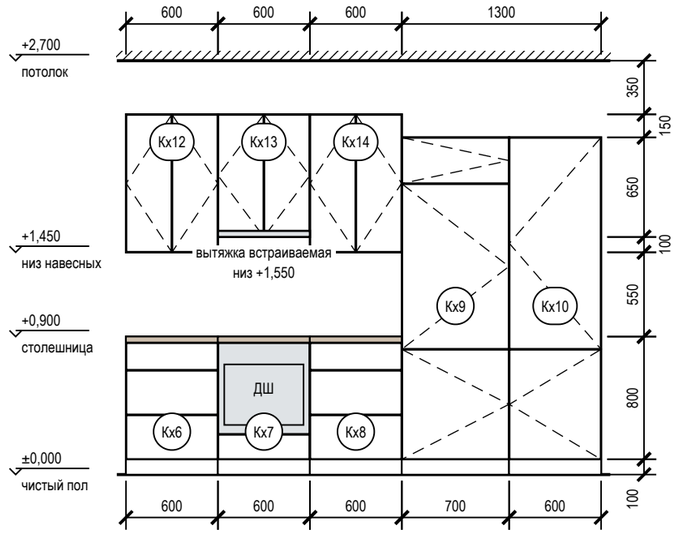


Вид без фасадов (наполнение, выводы)

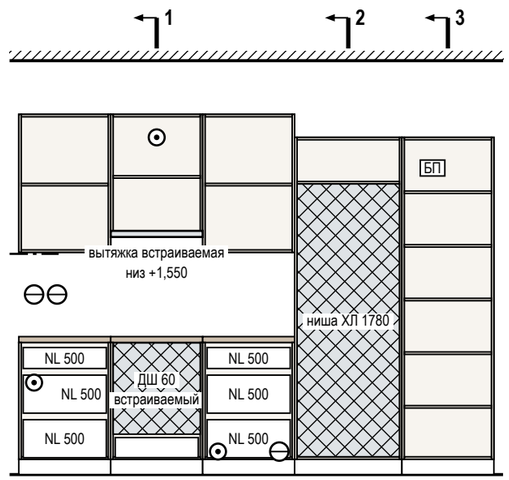


Разрез 1-1

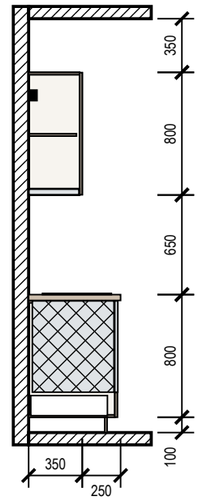

Разрез 2-2

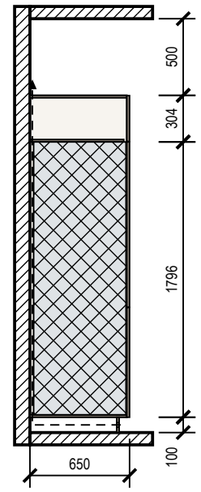

Разрез 3-3

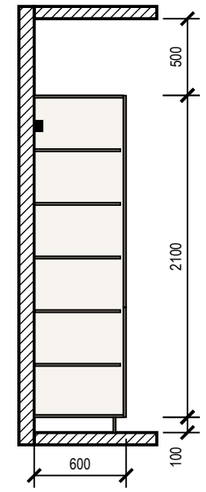

Условные обозначения

- фасад распашной: линии сходятся к стороне петель
- фасад ящика, карго
- встраиваемая техника
- столешница
- доборная планка
- деталь в разрезе
- К1 — марка изделия или модуля (на схеме расположения под ней — лист изделия)
- розетка на стене
- вывод кабеля к технике
- В1 — вывод воды В1 / Т3, канализации К1

Примечания

1. Размеры — в мм по чистовой отделке, вид из помещения; марки — как на плане расстановки. Перед раскроем — контрольный замер цеха после фартука и пола.
2. Корпуса — ЛДСП 16 мм, задняя стенка ХДФ 4 мм; фасады — МДФ, эмаль матовая 18 мм, цвет по колерной карте; столешница 38 мм, свес 20 мм; цоколь 100 мм.
3. Кромка: скрытые торцы 0,4 мм, видимые 2 мм. Номинальные зазоры: между фасадами 3 мм, фасад — столешница 3 мм, фасад — стена не менее 3 мм.
4. Ящики полного выдвижения и петли — с доводчиком; присадка по 32-й системе — выполняет цех.
5. Вытяжка встраивается в дно навесного модуля Кх13 над варочной: её низ на 1550 мм от пола, 650 мм над панелью (не меньше 650 мм).
6. Ниши техники (холодильник — ориентир 1780 мм) — по монтажным схемам выбранных моделей: решётка в цоколе и канал за пеналом холодильника, зазор за духовым шкафом, фасад ПММ на двери машины.

Допущения и предложения на листе

Основа листа: взаимное расположение помещений, контур дома 9600 × 8000 и раскладка этажей подобраны проектировщиком под габариты помещений брифа; обмер и проект АР — задание (К-1); высота потолка 2900 мм — по брифу, не замерена; перекрытие 330 мм и отметка 2-го этажа +3,230 приняты; проект КР — задание (К-2); наружные стены 400 мм, перегородки 120 мм приняты (в брифе толщин нет) (К-1); разрешённая мощность 15 кВт принята по типовым ТУ для частного дома (К-4); подрайон климата не задан — принят не северный (жилые от 2,5 м) (К-7).

См. лист открытых вопросов (лист 7, записи К-1, К-2, К-4; лист 8, запись К-7).

1000 мм · печать 1:1

Изм.	Кол.уч	Лист	№ док.	Подп.	Дата
Разраб.		Кырлан А.С.			04.11.26
Пров.					
ГИП					
Н. контр.					
Утв.					

ГД-2026-012-АИ

Дом 120 м²

Общая площадь 147,36* м² · * размеры приняты, не замерены (реестр — л. 7–9, К-1)

Дизайн-проект интерьера

Стадия	Лист	Листов
РП	109	175

Кухня (пом. 1). Развёртка гарнитура

М 1:40

Кырлан Александр Сергеевич


выпуск 04.11.2026 № 4dfa962484 · стр. 112 из 180

Кухня (пом. 1). Монтажная схема


Гостиная-кухня (пом. 1) · стена Б · размеры в мм от чистых поверхностей, высоты — от чистого пола

ПРЕДВАРИТЕЛЬНО · не для производства работ · открыто пунктов: 11 (реестр — л. 7–9)

Привязка выводов и крепление модулей

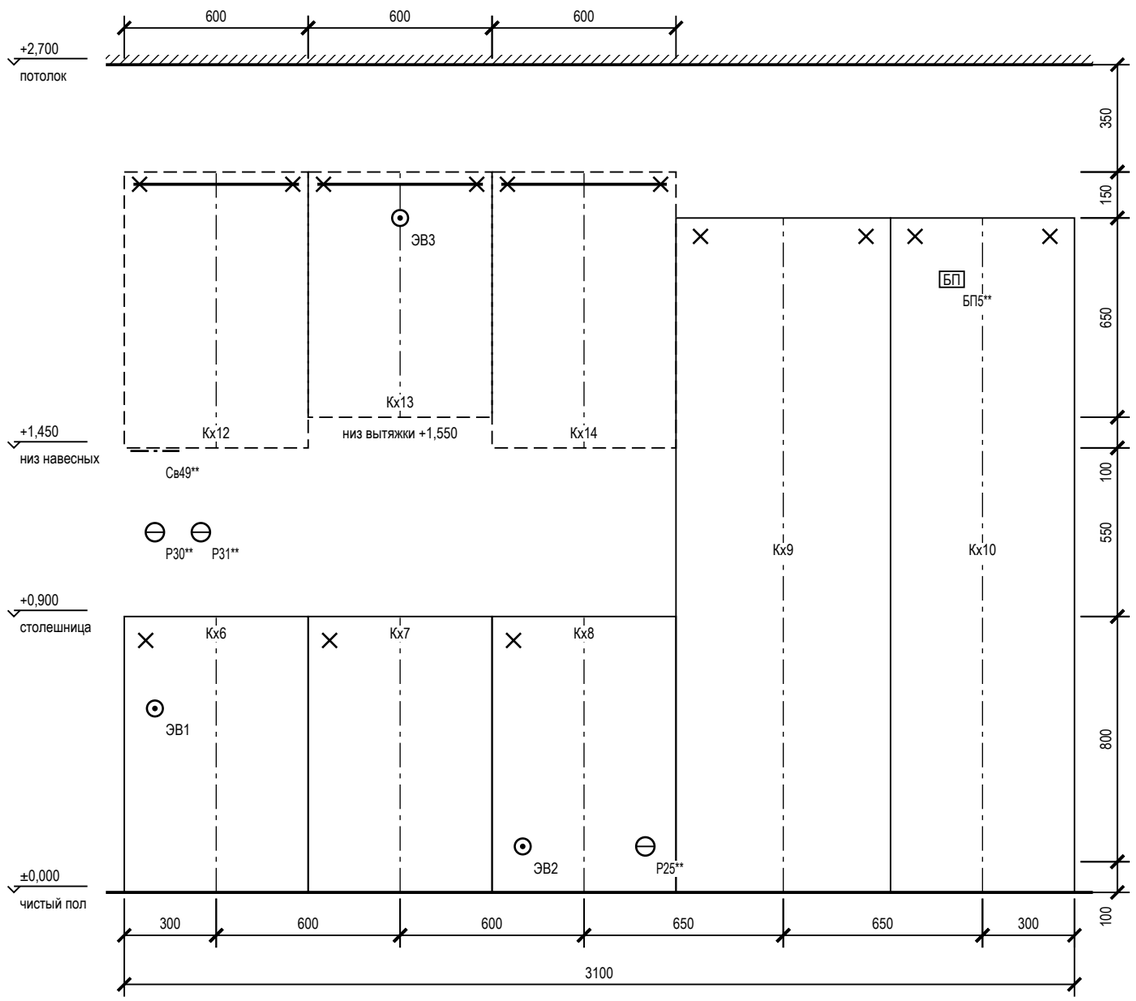

План столешницы

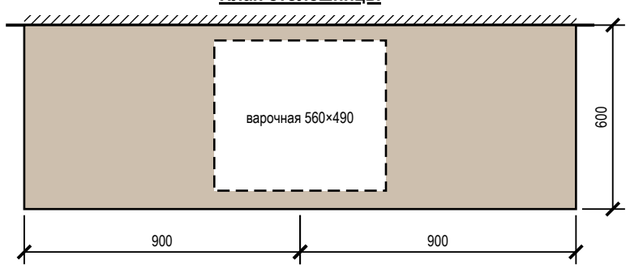

Привязка выводов к осям модулей

Код	Назначение	Модуль	От оси, мм	H, мм	Размещение
Р30**	розетка ×2 — фартук между мойкой и варочной	Кх6	−200	1175	над столешницей (фартук)
ЭВ1	вывод кабеля — варочная панель Кх7 (вывод в соседнем модуле Кх6, за ящиком)	Кх6	−200	600	в соседнем модуле, за ящиком
Св49**	светодиодная лента — подсветка столешницы	Кх6	−200	1440	в профиле по низу навесного модуля
Р31**	розетка — фартук между мойкой и варочной	Кх6	−50	1175	над столешницей (фартук)
ЭВ3	вывод кабеля — вытяжка	Кх13	0	2200	в навесном модуле
ЭВ2	вывод кабеля — духовой шкаф	Кх8	−200	150	в соседнем модуле, за ящиком
Р25**	розетка — холодильник Кх9 (розетка в соседнем модуле Кх8, съёмная панель)	Кх8	+200	150	в соседнем модуле, за ящиком
БП5**	блок питания — в пенале Кх10, верх, съёмная панель	Кх10	−100	2000	за пеналом

Зазоры под отделку

Поверхность	Отделка	Зазор, мм	Учесть
фартук	керамогранит	10	от чернового основания до корпуса навесных и столешницы
стены	окраска	5	под штукатурку и шпаклёвку за пеналом
пол	инженерная доска		цоколь — после укладки пола, опоры ±20 мм

Условные обозначения

- нижний модуль, пенал (контур)
- невидимый контур: навесной модуль, корпус под столешницей
- ось модуля (от неё — привязка вывода)
- анкер / уголок крепления к стене
- розетка на стене
- вывод кабеля к технике
- B1 — вывод воды В1 / Т3, канализации К1

Допущения и предложения на листе

Основа листа: взаимное расположение помещений, контур дома 9600 × 8000 и раскладка этажей подобраны проектировщиком под габариты помещений брифа; обмер и проект АР — задание (К-1); высота потолка 2900 мм — по брифу, не замерена; перекрытие 330 мм и отметка 2-го этажа +3,230 приняты; проект КР — задание (К-2); наружные стены 400 мм, перегородки 120 мм приняты (в брифе толщин нет) (К-1); разрешённая мощность 15 кВт принята по типовым ТУ для частного дома (К-4); подрайон климата не задан — принят не северный (жилые от 2,5 м) (К-7).
Знак «**» — предложение проектировщика, заказчиком не утверждено (согласовать с заказчиком): Р25 — высота 2000 мм выше нормы 1 м (ПУЭ 6.6.30) по назначению: питание встроенного холодильника Кх9, розетка над нишей за съёмной панелью; Р30, Р31 — Сдвиг под раскладку плитки фартука (стена Б) на 75 мм выше — ось на шве или в центре плитки, привязка по таблице листа; Св49, БП5 — диммируемость добавлена разработчиком проекта под светорегуляторы S10 и S11.
См. лист открытых вопросов (лист 7, записи К-1, К-2, К-4; лист 8, запись К-7).

Примечания

1. Выводы — по проекту электрики и ВК; привязка по горизонтали — от оси модуля (плюс — вправо по виду), по высоте — от чистого пола до оси вывода.
2. Пенал — уголки к стене 2 шт. сверху; нижние модули — стяжками между собой и уголком к стене; ряд выставить по уровню опорами цоколя.
3. Розетки над столешницей — не ниже 150 мм над ней и не за корпусом техники; розетка за ПММ, духовым шкафом и холодильником — только в соседнем модуле или в зоне цоколя с доступом.
4. Столешница — вырезы по шаблонам выбранных моделей мойки и варочной панели; торцы у стены — герметик, пристеночный плинтус.

1000 мм · печать 1:1

Изм.	Кол.уч	Лист	№ док.	Подп.	Дата
Разраб.		Кырлан А.С.			04.11.26
Пров.					
ГИП					
Н. контр.					
Утв.					

ГД-2026-012-АИ

Дом 120 м²

Общая площадь 147,36* м² · * размеры приняты, не замерены (реестр — л. 7–9, К-1)

Дизайн-проект интерьера

Стадия	Лист	Листов
РП	110	175

Кухня (пом. 1). Монтажная схема

М 1:20

Кырлан Александр Сергеевич


выпуск 04.11.2026 № 4dfa962484 · стр. 113 из 180

Шкафы. Монтажная схема. Лист 1 из 2


ПРЕДВАРИТЕЛЬНО · не для производства работ · открыто пунктов: 11 (реестр — л. 7–9)

крепление к стене, установочные размеры, зазоры под отделку · размеры в мм, отметки в м от ±0,000 (чистый пол 1-го этажа)


Шкаф-купе Пх1 (пом. 5)

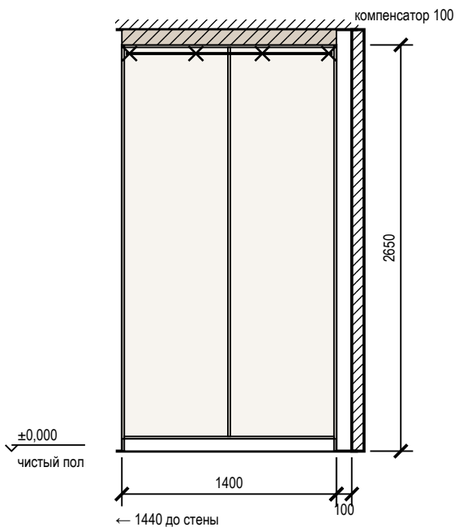


Шкаф распашной М4 (пом. 6)

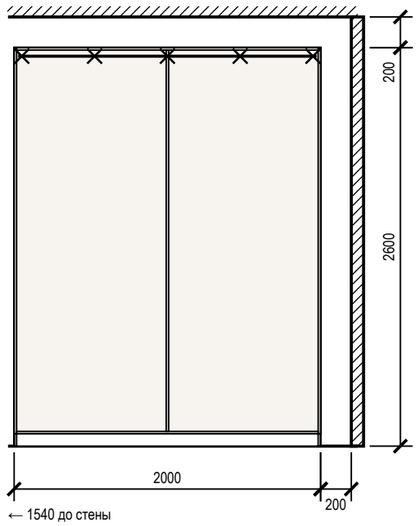


Шкаф распашной Дт3 (пом. 7)

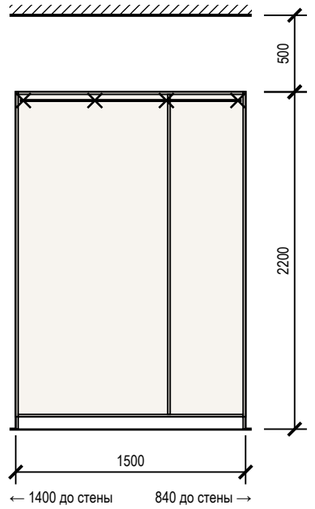

Система хранения Гд1 (пом. 8)

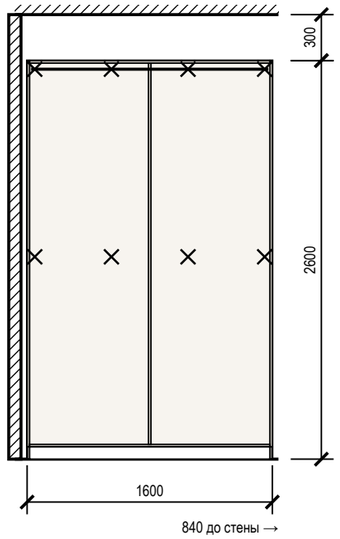

Система хранения Гд2 пом. 8

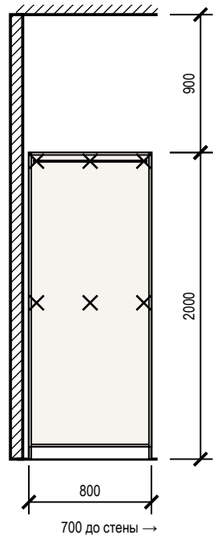

Крепление и зазоры под отделку (изделия листа 1)

Марка	Помещение, стена	Основание	Отделка стены	Зазор, мм	Крепёж по планке	От опрокидывания
Пх1	Прихожая (5), стена Б	по основанию — см. таблицу крепежа	окраска	5	анкер 4 шт., шаг 433	уголки 2 шт.
М4	Спальня родителей (6), стена В	по основанию — см. таблицу крепежа	окраска	5	анкер 5 шт., шаг 475	уголки 2 шт.
Дт3	Детская (7), стена А	по основанию — см. таблицу крепежа	окраска	5	анкер 4 шт., шаг 467	уголки 2 шт.
Гд1	Гардеробная (8), стена А	по основанию — см. таблицу крепежа	окраска	5	анкер 8 шт. (2 ряда)	уголки 2 шт.
Гд2	Гардеробная (8), стена Г	по основанию — см. таблицу крепежа	окраска	5	анкер 6 шт. (2 ряда)	уголки 2 шт.

Крепёж по основанию стены

Основание стены	Крепёж
бетон, ж/б	анкер-шуруп 7,5×72 или дюбель 8×60 с шурупом 5×70
кирпич полнотелый	дюбель 8×80 с шурупом 5×90
газобетон, пазогребень	дюбель для газобетона 10×100 или химический анкер
гипсокартон	закладная до обшивки (брус 40×80 или фанера 18 мм), саморез в закладную

Условные обозначения

- анкер / уголок крепления к стене
- корпус и полки ЛДСП (вид на стену)
- компенсатор — короб до потолка

Примечания

1. Установочные размеры — от чистого пола и чистых стен; перед установкой контрольный замер после отделки.
2. Порядок: корпус выставить по уровню опорами цоколя → закрепить к стене по задней планке → навесить двери и фасады, отрегулировать зазоры → подогнать и закрепить компенсатор.
3. Анкеры — с шагом не более 500 мм, не ближе 50 мм от края планки; на ГКЛ только в закладную, установленную до обшивки.
4. Скрытые коммуникации под анкеры проверить детектором; трассы электрики по плану розеток.
5. Монтажная схема на 2 листах, лист 1 из 2; продолжение — на следующем листе схемы. Условные обозначения, таблица крепежа по основанию и примечания повторены на каждом листе.

Допущения и предложения на листе

Основа листа: взаимное расположение помещений, контур дома 9600 × 8000 и раскладка этажей подобраны проектировщиком под габариты помещений брифа; обмер и проект АР — задание (К-1); высота потолка 2900 мм — по брифу, не замерена; перекрытие 330 мм и отметка 2-го этажа +3,230 приняты; проект КР — задание (К-2); наружные стены 400 мм, перегородки 120 мм приняты (в брифе толщин нет) (К-1); разрешённая мощность 15 кВт принята по типовым ТУ для частного дома (К-4); подрайон климата не задан — принят не северный (жилые от 2,5 м) (К-7).

См. лист открытых вопросов (лист 7, записи К-1, К-2, К-4; лист 8, запись К-7).

1000 мм · печать 1:1

Изм.	Кол.уч	Лист	№ док.	Подп.	Дата
Разраб.		Кырлан А.С.			04.11.26
Пров.					
ГИП					
Н. контр.					
Утв.					

ГД-2026-012-АИ

Дом 120 м²

Общая площадь 147,36* м² · * размеры приняты, не замерены (реестр — л. 7–9, К-1)

Дизайн-проект интерьера

Стадия	Лист	Листов
РП	111	175

Шкафы. Монтажная схема. Лист 1 из 2

М 1:40


Кырлан Александр Сергеевич

выпуск 04.11.2026 № 4dfa962484 · стр. 114 из 180


Шкафы. Монтажная схема. Лист 2 из 2

крепление к стене, установочные размеры, зазоры под отделку · размеры в мм, отметки в м от ±0,000 (чистый пол 1-го этажа)


Система хранения Кл1 (пом. 9)

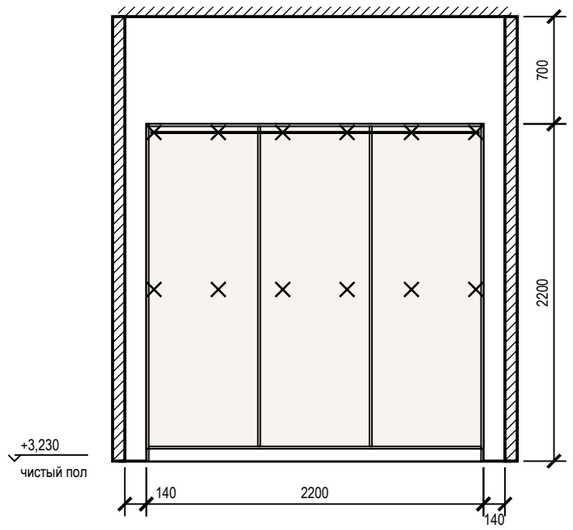


Система хранения Кл2 пом. 9

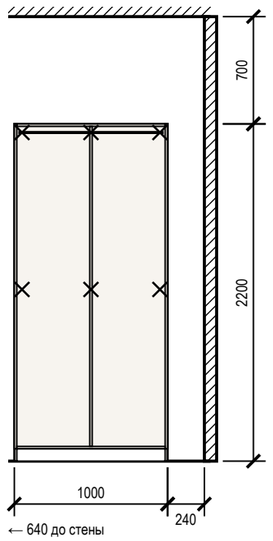

Шкаф распашной Дт8 пом. 12

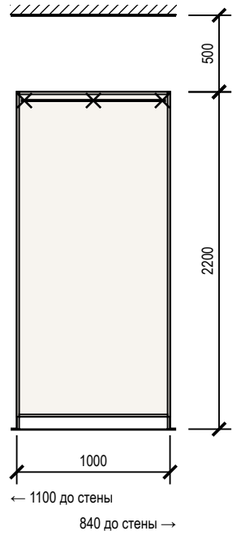

Система хранения Дт10 пом. 12

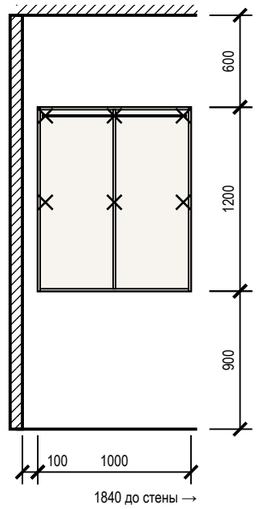

Крепление и зазоры под отделку (изделия листа 2)

Марка	Помещение, стена	Основание	Отделка стены	Зазор, мм	Крепёж по планке	От опрокидывания
Кл1	Кладовая (9), стена В	по основанию — см. таблицу крепежа	окраска	5	анкер 12 шт. (2 ряда)	уголки 2 шт.
Кл2	Кладовая (9), стена Г	по основанию — см. таблицу крепежа	окраска	5	анкер 6 шт. (2 ряда)	уголки 2 шт.
Дт8	Детская вторая (12), стена Г	по основанию — см. таблицу крепежа	окраска	5	анкер 3 шт., шаг 450	уголки 2 шт.
Дт10	Детская вторая (12), стена Г	по основанию — см. таблицу крепежа	окраска	5	анкер 6 шт. (2 ряда)	уголки 2 шт.

Крепёж по основанию стены

Основание стены	Крепёж
бетон, ж/б	анкер-шуруп 7,5×72 или дюбель 8×60 с шурупом 5×70
кирпич полнотелый	дюбель 8×80 с шурупом 5×90
газобетон, пазогребень	дюбель для газобетона 10×100 или химический анкер
гипсокартон	закладная до обшивки (брус 40×80 или фанера 18 мм), саморез в закладную

Условные обозначения

- анкер / уголок крепления к стене
- корпус и полки ЛДСП (вид на стену)
- компенсатор — короб до потолка

Примечания

1. Установочные размеры — от чистого пола и чистых стен; перед установкой контрольный замер после отделки.
2. Порядок: корпус выставить по уровню опорами цоколя → закрепить к стене по задней планке → навесить двери и фасады, отрегулировать зазоры → подогнать и закрепить компенсатор.
3. Анкеры — с шагом не более 500 мм, не ближе 50 мм от края планки; на ГКЛ только в закладную, установленную до обшивки.
4. Скрытые коммуникации под анкеры проверить детектором; трассы электрики по плану розеток.
5. Монтажная схема на 2 листах, лист 2 из 2. Условные обозначения, таблица крепежа по основанию и примечания повторены на каждом листе.

Допущения и предложения на листе

Основа листа: взаимное расположение помещений, контур дома 9600 × 8000 и раскладка этажей подобраны проектировщиком под габариты помещений брифа; обмер и проект АР — задание (К-1); высота потолка 2900 мм — по брифу, не замерена; перекрытие 330 мм и отметка 2-го этажа +3,230 приняты; проект КР — задание (К-2); наружные стены 400 мм, перегородки 120 мм приняты (в брифе толщин нет) (К-1); разрешённая мощность 15 кВт принята по типовым ТУ для частного дома (К-4); подрайон климата не задан — принят не северный (жилые от 2,5 м) (К-7).

Знак «*» — принято, не замерено и не подтверждено (замерить на объекте): К-2: отметка чистого пола этажа «2-й этаж» +3,230 — отметка чистого пола 2-го этажа +3,230 принята: высота потолка 2900 по брифу + перекрытие с полом 330 (конструкция перекрытия не задана; проект КР — задание).

См. лист открытых вопросов (лист 7, записи К-1, К-2, К-4; лист 8, запись К-7).

1000 мм · печать 1:1

Изм.	Кол.уч	Лист	№ док.	Подп.	Дата
Разраб.		Кырлан А.С.			04.11.26
Пров.					
ГИП					
Н. контр.					
Утв.					

ГД-2026-012-АИ

Дом 120 м²

Общая площадь 147,36* м² · * размеры приняты, не замерены (реестр — л. 7–9, К-1)

Дизайн-проект интерьера

Стадия	Лист	Листов
РП	112	175

Шкафы. Монтажная схема. Лист 2 из 2

М 1:40

Кырлан Александр Сергеевич

Ведомости изделий, техники и фурнитуры

встроенная мебель и кухонный гарнитур · размеры в мм

Ведомость изделий

Марка	Наименование	Пом.	Ш×Г×В, мм	Корпус	Фасад	Кромка, мм	Кол.
Пх1	Шкаф-купе	5	1400×600×2650	ЛДСП 16	ЛДСП 10 мм в алюминиевом профиле	0,4 / 2	1
М4	Шкаф распашной	6	2000×600×2600	ЛДСП 16	МДФ 18 мм, эмаль матовая	0,4 / 2	1
Дт3	Шкаф распашной	7	1500×600×2200	ЛДСП 16	МДФ 18 мм, эмаль матовая	0,4 / 2	1
Гд1	Система хранения	8	1600×600×2600	ЛДСП 16	без фасадов	0,4 / 2	1
Гд2	Система хранения	8	800×400×2000	ЛДСП 16	без фасадов	0,4 / 2	1
Кл1	Система хранения	9	2200×400×2200	ЛДСП 16	без фасадов	0,4 / 2	1
Кл2	Система хранения	9	1000×400×2200	ЛДСП 16	без фасадов	0,4 / 2	1
Дт8	Шкаф распашной	12	1000×600×2200	ЛДСП 16	МДФ 18 мм, эмаль матовая	0,4 / 2	1
Дт10	Система хранения	12	1000×300×1200	ЛДСП 16	без фасадов	0,4 / 2	1
Кх1	Модуль нижний: ящики	1	600×600×900	ЛДСП 16	МДФ 18 мм, эмаль матовая	0,4 / 2	1
Кх2	Модуль нижний: мойка	1	800×600×900	ЛДСП 16	МДФ 18 мм, эмаль матовая	0,4 / 2	1
Кх3	Модуль под ПММ 60: без корпуса, фасад на дверь машины	1	600×600×900	без корпуса	МДФ 18 мм, эмаль матовая — на дверь машины (навеска из её комплекта), цоколь		1
Кх11	Модуль навесной: полки	1	600×350×900	ЛДСП 16	МДФ 18 мм, эмаль матовая	0,4 / 2	1
Кх5	Модуль нижний: ящики	1	1040×600×900	ЛДСП 16	МДФ 18 мм, эмаль матовая	0,4 / 2	1
Кх6	Модуль нижний: ящики	1	600×600×900	ЛДСП 16	МДФ 18 мм, эмаль матовая	0,4 / 2	1
Кх12	Модуль навесной: полки	1	600×350×900	ЛДСП 16	МДФ 18 мм, эмаль матовая	0,4 / 2	1
Кх7	Модуль нижний: духовой шкаф, варочная	1	600×600×900	ЛДСП 16	МДФ 18 мм, эмаль матовая	0,4 / 2	1
Кх13	Модуль навесной: полки	1	600×350×800	ЛДСП 16	МДФ 18 мм, эмаль матовая	0,4 / 2	1
Кх8	Модуль нижний: ящики	1	600×600×900	ЛДСП 16	МДФ 18 мм, эмаль матовая	0,4 / 2	1
Кх14	Модуль навесной: полки	1	600×350×900	ЛДСП 16	МДФ 18 мм, эмаль матовая	0,4 / 2	1
Кх9	Пенал: холодильник встр.	1	700×650×2200	ЛДСП 16	МДФ 18 мм, эмаль матовая	0,4 / 2	1
Кх10	Пенал: полки	1	600×600×2200	ЛДСП 16	МДФ 18 мм, эмаль матовая	0,4 / 2	1

Ведомость встраиваемой техники

Поз.	Прибор	Ниша, вырез, мм	Вентиляция	Питание	Схема
Кх2	Мойка врезная / подстольная с сифоном	вырез по шаблону, ориентир 700 × 480		смеситель — выводы ВК	по модели
Кх3	Посудомоечная машина встраиваемая, 60 см	ниша 600 × 862 (от пола до низа столешницы)	зазор в цоколе, по схеме	Р32: Кх5.1, Н=300 — в соседнем модуле, за ящиком	по модели
Кх7	Духовой шкаф встраиваемый, 60 см	ниша 560 × 600, глубина ≥ 550	зазор за шкафом, вырез в задней стенке	ЭВ2: Кх8, Н=150 — в соседнем модуле, за ящиком	по модели
Кх7	Варочная панель индукционная, 60 см	вырез в столешнице 560 × 490		Р31**: Кх6, Н=1175 — над столешницей (фартук)	по модели
Кх9	Холодильник встраиваемый, ниша 1780	ниша 1780 × 560 × 550	решётка в цоколе, канал за корпусом, выход сверху	Р25**: Кх8, Н=150 — в соседнем модуле, за ящиком	по модели
Кх13	Вытяжка встраиваемая в навесной модуль, 60 см	низ ≥ 650 над панелью	воздуховод к вентканалу, короб до потолка	ЭВ3: Кх13, Н=2200 — в навесном модуле	по модели

Допущения и предложения на листе. Основа листа: взаимное расположение помещений, контур дома 9600 × 8000 и раскладка этажей подобраны проектировщиком под габариты помещений брифа; обмер и проект АР — задание (К-1); высота потолка 2900 мм — по брифу, не замерена; перекрытие 330 мм и отметка 2-го этажа +3,230 приняты; проект КР — задание (К-2); наружные стены 400 мм, перегородки 120 мм приняты (в брифе толщин нет) (К-1); разрешённая мощность 15 кВт принята по типовым ТУ для частного дома (К-4); подрайон климата не задан — принят не северный (жилые от 2,5 м) (К-7). Знак «**» — предложение проектировщика, заказчиком не утверждено (согласовать с заказчиком): Р25 — высота 2000 мм выше нормы 1 м (ПУЭ 6.6.30) по назначению: питание встроенного холодильника Кх9, розетка над нишей за съёмной панелью; Р31 — Сдвиг под раскладку плитки фартука (стена Б) на 75 мм выше — ось на шве или в центре плитки, привязка по таблице листа. См. лист открытых вопросов (лист 7, записи К-1, К-2, К-4; лист 8, запись К-7).

Ведомость фурнитуры

№	Фурнитура	Тип, размер	Изделия	Кол.
1	Система дверей купе: профиль, направляющие, ролики	на 2 двери	Пх1	1
2	Ручка-профиль вертикальная	в цвет профиля	Пх1	2
3	Полкодержатель с фиксацией	ø5 мм	Пх1, М4, Дт3, Гд1, Кл1, Кл2, Дт8, Дт10, Кх11, Кх12, Кх13, Кх14, Кх9, Кх10	228
4	Штанга овальная 30×15, L = 676	+ 2 держателя	Пх1	1
5	Полка для обуви выдвижная наклонная	ширина 676	Пх1	3
6	Опора регулируемая с цоколем на клипсах	ход 20 мм	Пх1, М4, Дт3, Гд1, Гд2, Кл1, Кл2, Дт8	50
7	Анкер по основанию стены	по таблице крепежа	Пх1, М4, Дт3, Гд1, Гд2, Кл1, Кл2, Дт8, Дт10, Кх11, Кх12, Кх13, Кх14	62
8	Уголок крепления к стене от опрокидывания	стальной	Пх1, М4, Дт3, Гд1, Гд2, Кл1, Кл2, Дт8, Дт10, Кх9, Кх10	22
9	Петля накладная 110° с доводчиком	чашка 35 мм	М4, Дт3, Дт8, Кх2, Кх11, Кх12, Кх13, Кх14, Кх9, Кх10	86
10	Штанга овальная 30×15, L = 976	+ 2 держателя	М4, Дт3	2
11	Штанга овальная 30×15, L = 776	+ 2 держателя	Гд1	1
12	Штанга выдвижная торцевая	L по глубине	Гд2, Кл1, Кл2	5
13	Штанга овальная 30×15, L = 968	+ 2 держателя	Дт8	1
14	Направляющие полного выдвижения с доводчиком NL 500	пара	Кх1, Кх5, Кх6, Кх7, Кх8	16
15	Ручка-профиль	латунь матовая	Кх1, Кх2, Кх3, Кх11, Кх5, Кх6, Кх12, Кх7, Кх13, Кх8, Кх14, Кх9, Кх10	32
16	Опора кухонная регулируемая 100–120 мм	+ клипса цоколя	Кх1, Кх2, Кх5, Кх6, Кх7, Кх8, Кх9, Кх10	38
17	Комплект навески фасада ПММ	из поставки машины	Кх3	1
18	Навес регулируемый для навесного шкафа	пара на секцию	Кх11, Кх12, Кх13, Кх14	4
19	Шина монтажная	L = 540	Кх11, Кх12, Кх13, Кх14	4

Примечания

1. Модели техники выбирает заказчик до изготовления мебели; ниши, вырезы и вентиляция — по монтажной схеме выбранной модели (условие гарантии), её номер вносится в ведомость.
2. Количество фурнитуры — по чертежам изделий; запас крепежа 5 %. Аналоги — по характеристикам (доводчик, нагрузка, ход).
3. Цвет корпусов, фасадов и профилей — по колерной карте проекта. Кромка — скрытые / видимые торцы, мм.

Изм.	Кол.уч	Лист	№ док.	Подп.	Дата
Разраб.		Кырлан А.С.			04.11.26
Пров.					
ГИП					
Н. контр.					
Утв.					

ГД-2026-012-АИ

Дом 120 м²

Общая площадь 147,36* м² · * размеры приняты, не замерены (реестр — л. 7–9, К-1)

Дизайн-проект интерьера

Стадия	Лист	Листов
РП	113	175

Ведомости изделий, техники и фурнитуры

М б/м

Кырлан Александр Сергеевич

выпуск 04.11.2026 № 4dfa962484 · стр. 116 из 180

04

Развёртки и узлы



Кырлан Александр Сергеевич

выпуск 04.11.2026 № 4dfa962484 · стр. 117 из 180

Реестр марок отделки и позиций альбома

Реестр марок отделки (О ↔ позиции колерной карты) и марки позиций по видам

ПРЕДВАРИТЕЛЬНО · не для производства работ · открыто пунктов: 11 (реестр — л. 7–9)

Реестр марок отделки альбома

Марка	Поверхность	Материал, изделие	Цвет, код	Помещения	Колер. карта
О1	стены	окраска, Tikkurila, матовая, подготовка Q3	Tikkurila G503 «Calla»	1, 2, 3, 5, 6, 7, 10, 11, 12	К1, К8
О2	фартук	керамогранит, 1200×600×9 мм, аналог: керамогранит под травертин, матовый, затирка CG2WA		1	КМ2
О3	акцентная стена	окраска, Tikkurila, матовая, подготовка Q3	NCS S 3050-R80B «Эгейский синий»	1	К2
О4	плинтус	плинтус МДФ, h 80 мм, аналог: плинтус МДФ под покраску 80×16	Tikkurila G503 «Calla»	1, 2, 3, 5, 6, 10, 11	К4
О5	потолок	окраска, Little Greene Absolute Matt, глубокоматовая, подготовка Q3	Little Greene No. 222 «Loft White»	1, 2, 3, 5, 6, 7, 8, 10, 11, 12	К3
О6	пол	инженерная доска, Coswick Вековые традиции, 2100×127 мм, 1167-4250		1, 2, 3, 6, 7, 8, 9, 10, 11, 12	КМ1
О7	акцентная стена	окраска, Tikkurila, матовая, подготовка Q3	NCS S 5020-G90Y «Олива»	3	К5
О8	стены	облицовка плиткой, Atlas Concorde Marvel Travertine, 600×1200×9 мм, A8UZ, затирка CG2WA	Atlas Concorde A8UZ «Marvel Travertine»	4, 13	КМ3
О9	потолок	окраска, Little Greene Intelligent Bathroom, матовая, подготовка Q3	Little Greene No. 222 «Loft White»	4, 13	К6
О10	пол	керамогранит, 600×600×9 мм, аналог: керамогранит ректифицированный под травертин, матовый, затирка CG2WA		4, 13	КМ4
О11	пол	керамогранит, Atlas Concorde Marvel Travertine, 600×1200×9 мм, A8UZ, затирка CG2WA	Atlas Concorde A8UZ «Marvel Travertine»	5	КМ5
О12	акцентная стена	окраска, Farrow & Ball Modern Emulsion, матовая, подготовка Q3	Farrow & Ball No. 89 «Lulworth Blue светлая морская лазурь»	6	К7
О13	акцентная стена	окраска, Farrow & Ball, шелковисто-матовая, подготовка Q3	Farrow & Ball No. 66 «India Yellow — охра / горчица итальянских фасадов»	7	К9
О14	плинтус	плинтус МДФ, Orac Decor Contour (Luxxus), h 69 мм, SX165	Tikkurila G503 «Calla»	7, 12	К10
О15	стены	окраска, Little Greene Intelligent Matt, матовая, подготовка Q3	Little Greene No. 222 «Loft White»	8	К11
О16	плинтус	плинтус МДФ, h 80 мм, аналог: плинтус МДФ под покраску 80×16	Little Greene No. 222 «Loft White»	8	К12
О17	стены	окраска, Tikkurila, матовая, подготовка Q3	NCS S 0502-Y	9	К13
О18	плинтус	плинтус МДФ, Orac Decor Contour (Luxxus), h 69 мм, SX165, шелковисто-матовая	NCS S 0300-N	9	К15
О19	потолок	окраска, Tikkurila, глубокоматовая	NCS S 0300-N	9	К14
О20	акцентная стена	окраска, Tikkurila, шелковисто-матовая, подготовка Q3	Tikkurila H440 «H440 Wave — бирюзово-голубая вода»	12	К16

Допущения и предложения на листе. Основа листа: взаимное расположение помещений, контур дома 9600 × 8000 и раскладка этажей подобраны проектировщиком под габариты помещений брифа; обмер и проект АР — задание (К-1); высота потолка 2900 мм — по брифу, не замерена; перекрытие 330 мм и отметка 2-го этажа +3,230 приняты; проект КР — задание (К-2); наружные стены 400 мм, перегородки 120 мм приняты (в брифе толщин нет) (К-1); разрешённая мощность 15 кВт принята по типовым ТУ для частного дома (К-4); подрайон климата не задан — принят не северный (жилые от 2,5 м) (К-7). Знак «*» — принято, не замерено (замерить): К-5: Ст К1-1, Ст В1-1, Ст Т3-1, Ст К1-2 (кухня), Ст В1-2. Знак «**» — предложено, не утверждено (согласовать): плинтус пом. 1–3, 5, 6, 8, 10, 11, фартук пом. 1, пол пом. 4, 13, S10, S11, P18, P19, P25, P26, P27, P28, P29, P30, P31, Св42, Св43, Св44, Св49, БП5, ИП6, Св52, ЭВ5, КУП2, S15, Св30, ИП3, ИП9, ИП7, ЭВ4, АР2, АР1; ИЗ-1: См1, См2, См3, См5, Св15, КУП1; ИЗ-1, ИЗ-2: Р7, Р8, ЭВ6; ИЗ-2: Хл1, Кб1, Р33, Р17, Дт2, Хл2, Дт7, ЩС; К-9: См4. См. лист открытых вопросов (лист 7, записи К-1, К-2, К-4, К-5; лист 8, записи К-7, К-9; лист 9, записи ИЗ-1, ИЗ-2).

Марки позиций альбома по видам

Префикс	Что обозначает, позиции	Листы
Д, Д-вх	двери: Д-1–Д-10, Д-вх	17–24
Пр	проёмы без полотна (порталы): Пр-1	17–24
ОК	окна: ОК-1–ОК-6	17–24
Гд, Гс, Дт, Кб, Кл, Кх, М, Пх, Хл	мебель и оборудование: Гд1, Гд2, Гс1–Гс5, Дт1, Дт2**, Дт3–Дт6, Дт7**, Дт8–Дт10, Кб1**, Кб2–Кб4, Кл1, Кл2, Кх1–Кх3, Кх5–Кх15, М1–М6, Пх1, Пх2, Хл1**, Хл2**	25–33
Сг, См	сантехнические приборы: Сг1, Сг2, См1**, См2**, См3**, См4**, См5**	52–63
ДК	декор (картины, зеркала, растения): ДК1–ДК12, ДК40, ДК41, ДК43–ДК46	1, 88–95
Т	текстиль (шторы, ковры): Т1–Т31	1, 88–95
S	выключатели: S1–S9, S10**, S11**, S12–S14, S15**, S16–S21	34–47
Р	розетки: Р1–Р6, Р7**, Р8**, Р9–Р11, Р13–Р16, Р17**, Р18**, Р19**, Р20–Р24, Р25**, Р26**, Р27**, Р28**, Р29**, Р30**, Р31**, Р32, Р33**, Р34, Р40–Р49	34–47
ТВ	розетки ТВ: ТВ1	34–47
LAN	розетки компьютерные: LAN2–LAN5	34–47
ЭВ	выводы кабеля: ЭВ1–ЭВ3, ЭВ4**, ЭВ5**, ЭВ6**	34–47
АР	точки доступа Wi-Fi: АР1**, АР2**	34–47
Св	светильники: Св1–Св14, Св15**, Св16–Св29, Св30**, Св31–Св41, Св42**, Св43**, Св44**, Св45–Св48, Св49**, Св50, Св51, Св52**, Св53, Св54, Св80, Св82–Св102	34–47
БП	блоки питания LED: БП1–БП4, БП5**, БП6, БП7	34–47
ИП	извещатели: ИП1, ИП2, ИП3**, ИП4, ИП5, ИП6**, ИП7**, ИП8, ИП9**, ИП10	34–47
КУП	электроустановочные изделия: КУП1**, КУП2**	34–47
ЩК, ЩС**	щиты: ЩК, ЩС**	34–47
ДФ	домофон: ДФ1	34–47
Ст В1, Ст К1, Ст К1-2 (кухня), Ст Т3	стояки (системы В1, Т3, К1): Ст В1-1*, Ст В1-2*, Ст К1-1*, Ст К1-2 (кухня)*, Ст Т3-1*, Ст Т3-2	52–63
О	марки отделки (реестр альбома): О1–О20	2–6, 114–168
К, КМ	позиции колерной карты: К1–К16, КМ1–КМ5	83–87
Рд	радиаторы отопления: Рд1–Рд8	48–51

Изм.	Кол.уч	Лист	№ док.	Подп.	Дата
Разраб.		Кырлан А.С.			04.11.26
Пров.					
ГИП					
Н. контр.					
Утв.					

ГД-2026-012-АИ

Дом 120 м²

Общая площадь 147,36* м² · * размеры приняты, не замерены (реестр — л. 7–9, К-1)

Дизайн-проект интерьера

Стадия	Лист	Листов
РП	114	175

Реестр марок отделки и позиций альбома

М б/м

Кырлан Александр Сергеевич

выпуск 04.11.2026 № 4dfa962484 · стр. 118 из 180

Реестр марок отделки и позиций альбома (продолжение)

Реестр марок отделки (О ↔ позиции колерной карты) и марки позиций по видам

Примечания

1. Марка отделки О — одна на весь альбом: одна и та же отделка (материал, изделие, цвет, формат) на всех листах имеет одну марку; на развёртках и планах стоят марки этого реестра.
2. Столбец «Колер. карта» — позиции колерной карты (лист 83): К — окраска по коду цвета, КМ — материал без кода цвета; «Помещения» — номера по экспликации; количества — по ведомости отделки помещений (лист 80).
3. Марки позиций: один префикс — один вид позиций на весь альбом (двери Д, окна ОК, мебель М, сантехприборы П, декор ДК, текстиль Т, колерная карта К и КМ, радиаторы РО, розетки Р, выключатели S, светильники Св; стояки — «Ст» и система, например «Ст К1-1*»). Совпадение префиксов у разных видов — замечание к исходным данным, при выпуске исправляется в модели.

Допущения и предложения на листе

Основа листа: взаимное расположение помещений, контур дома 9600 × 8000 и раскладка этажей подобраны проектировщиком под габариты помещений брифа; обмер и проект АР — задание (К-1); высота потолка 2900 мм — по брифу, не замерена; перекрытие 330 мм и отметка 2-го этажа +3,230 приняты; проект КР — задание (К-2); наружные стены 400 мм, перегородки 120 мм приняты (в брифе толщин нет) (К-1); разрешённая мощность 15 кВт принята по типовым ТУ для частного дома (К-4); подрайон климата не задан — принят не северный (жилые от 2,5 м) (К-7).

Знак «*» — принято, не замерено и не подтверждено (замерить на объекте): К-5: Ст К1-1 — положение стояка принято проектировщиком (проект ВК дома не передан), не замерено.

Знак «**» — предложение проектировщика, заказчиком не утверждено (согласовать с заказчиком): плинтус пом. 1–3, 5, 6, 8, 10, 11, фартук пом. 1 — артикул изделия не выбран: позиция описана характеристиками («аналог по характеристикам»), артикул выбирается при закупке; пол пом. 4, 13 — пирог пола: стяжка 33 мм и обмазочная гидроизоляция добавлены разработчиком проекта; артикул изделия не выбран: позиция описана характеристиками («аналог по характеристикам»), артикул выбирается при закупке.

См. лист открытых вопросов (лист 7, записи К-1, К-2, К-4, К-5; лист 8, запись К-7).

Изм.	Кол.уч	Лист	№ док.	Подп.	Дата
Разраб.		Кырлан А.С.			04.11.26
Пров.					
ГИП					
Н. контр.					
Утв.					

ГД-2026-012-АИ

Дом 120 м²

Общая площадь 147,36* м² · * размеры приняты, не замерены (реестр — л. 7–9, К-1)

Дизайн-проект интерьера	Стадия	Лист	Листов
	РП	115	175

Реестр марок отделки и позиций альбома (продолжение)

М б/м


Кырлан Александр Сергеевич

выпуск 04.11.2026 № 4dfa962484 · стр. 119 из 180

Схема расположения развёрток и узлов · 1-й этаж

План этажа «1-й этаж»: марки развёрток по помещениям, выноски узлов, ведомость «марка → лист»

ПРЕДВАРИТЕЛЬНО · не для производства работ · открыто пунктов: 11 (реестр — л. 7–9)

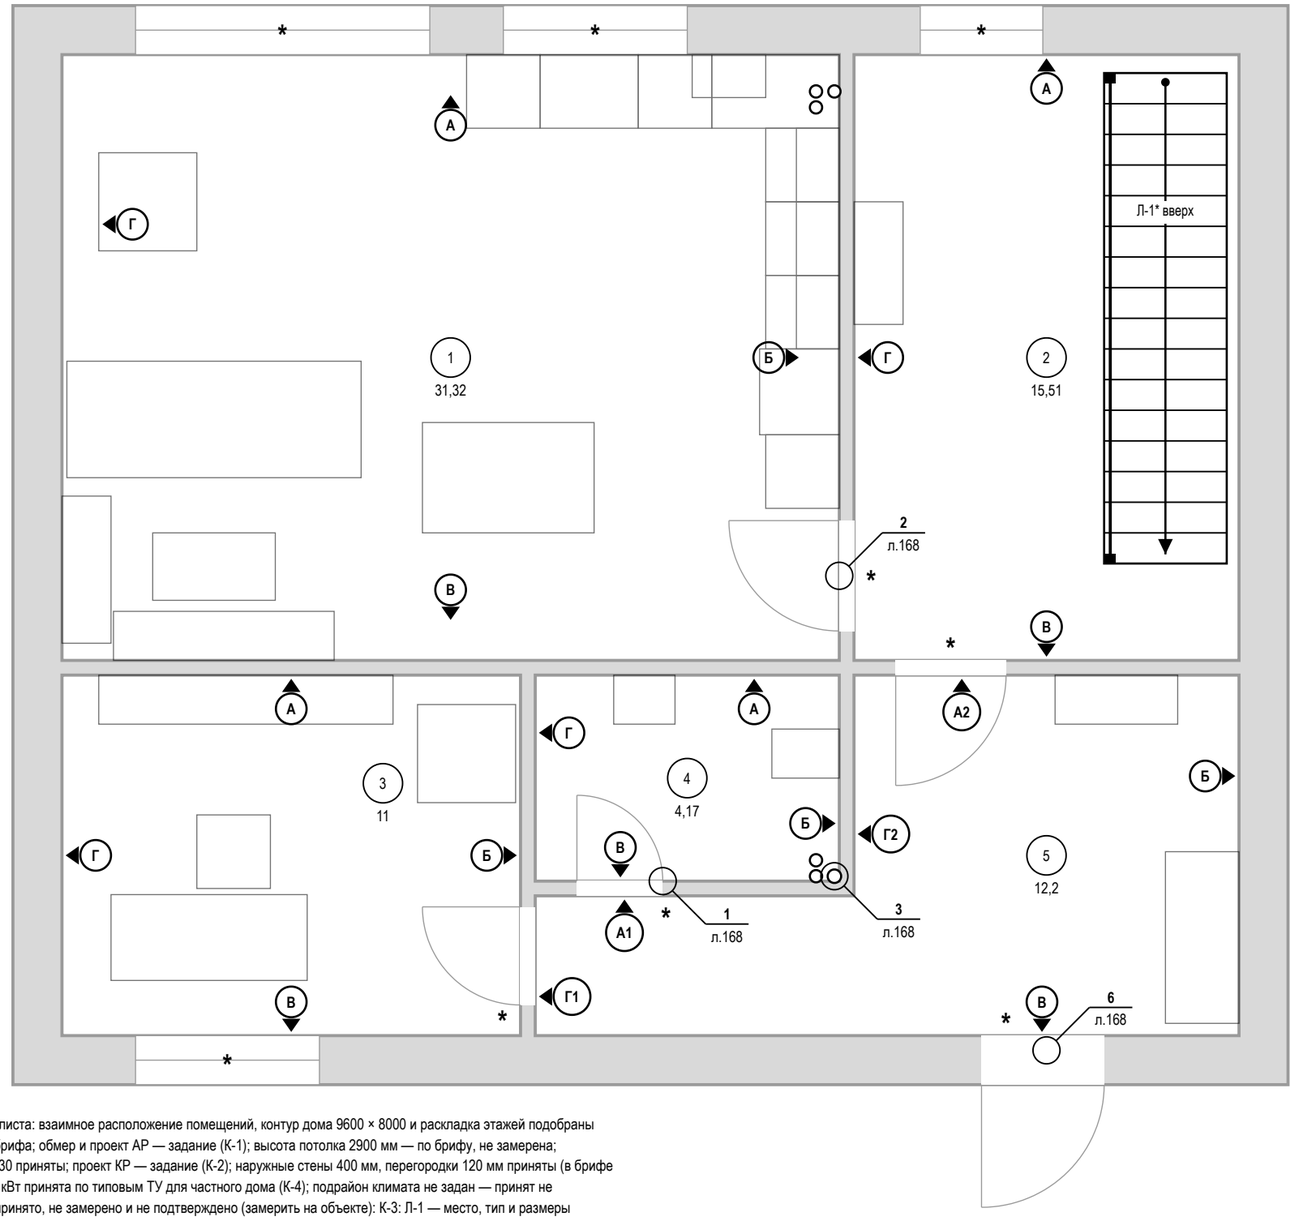

Допущения и предложения на листе. Основа листа: взаимное расположение помещений, контур дома 9600 × 8000 и раскладка этажей подобраны проектировщиком под габариты помещений брифа; обмер и проект АР — задание (К-1); высота потолка 2900 мм — по брифу, не замерена; перекрытие 330 мм и отметка 2-го этажа +3,230 приняты; проект КР — задание (К-2); наружные стены 400 мм, перегородки 120 мм приняты (в брифе толщин нет) (К-1); разрешённая мощность 15 кВт принята по типовым ТУ для частного дома (К-4); подрайон климата не задан — принят не северный (жилые от 2,5 м) (К-7). Знак «*» — принято, не замерено и не подтверждено (замерить на объекте): К-3: Л-1 — место, тип и размеры лестницы брифом не заданы (только «лестница из холла 1-го этажа»): одномаршевая 17 × 190 × 250 вдоль стены Б холла — предложение проектировщика; конструкция и расчёт — проект КР; К-5: Ст К1-1, Ст В1-1, Ст Т3-1, Ст К1-2 (кухня), Ст В1-2, Ст Т3-2 — положение стояка принято проектировщиком (проект ВК дома не передан), не замерено. См. лист открытых вопросов (лист 7, записи К-1–К-5; лист 8, запись К-7).

Развёртки и узлы: марка → лист

Марка	Помещение / узел	Лист
А	Гостиная-кухня (пом. 1)	118, 119
Б	Гостиная-кухня (пом. 1)	121, 122
В	Гостиная-кухня (пом. 1)	123, 124
Г	Гостиная-кухня (пом. 1)	126
А	Холл с лестницей (пом. 2)	127
В	Холл с лестницей (пом. 2)	128
Г	Холл с лестницей (пом. 2)	129
А	Кабинет (пом. 3)	130
Б	Кабинет (пом. 3)	131
В	Кабинет (пом. 3)	132
Г	Кабинет (пом. 3)	133
А, Б	Санузел гостевой (пом. 4)	134, 135
В, Г	Санузел гостевой (пом. 4)	136
А1	Прихожая (пом. 5)	137
А2	Прихожая (пом. 5)	138
Б	Прихожая (пом. 5)	139
В	Прихожая (пом. 5)	140
Г1, Г2	Прихожая (пом. 5)	142
узел 1	Порог 15 мм: мокрая зона — смежное помещение	168
узел 2	Дверь скрытого монтажа в плоскости стены, плинтус	168
узел 3	Короб стояков К1-1 с люком и звукоизоляцией	168
узел 6	Плинтус МДФ 80×16 мм у окрашенной стены по керамограниту (плитке)	168

Условные обозначения

- А — марка развёртки: буква стены, стрелка — взгляд
- выноска узла: над полкой — узел, под полкой — лист
- 1 — номер помещения, площадь м²

1000 мм · печать 1:1

Примечания

1. Развёртки — вид на стену изнутри помещения; буквы стен — одна система на весь альбом (как на листах выводов, плитки и отделки).
2. Стены без электроточек, мебели, декора и акцентной отделки развёрток не имеют: их отделка — по ведомости отделки помещений.
3. Узлы — на листе узлов; места применения — по выноскам этого листа и ведомости «марка → лист».

Изм.	Кол.уч	Лист	№ док.	Подп.	Дата
Разраб.		Кырлан А.С.			04.11.26
Пров.					
ГИП					
Н. контр.					
Утв.					

ГД-2026-012-АИ

Дом 120 м²

Общая площадь 147,36* м² · * размеры приняты, не замерены (реестр — л. 7–9, К-1)

Дизайн-проект интерьера

Стадия	Лист	Листов
РП	116	175

Схема расположения развёрток и узлов · 1-й этаж

М 1:50


Кырлан Александр Сергеевич

выпуск 04.11.2026 № 4dfa962484 · стр. 120 из 180

Схема расположения развёрток и узлов · 2-й этаж

План этажа «2-й этаж»: марки развёрток по помещениям, выноски узлов, ведомость «марка → лист»

ПРЕДВАРИТЕЛЬНО · не для производства работ · открыто пунктов: 11 (реестр — л. 7–9)

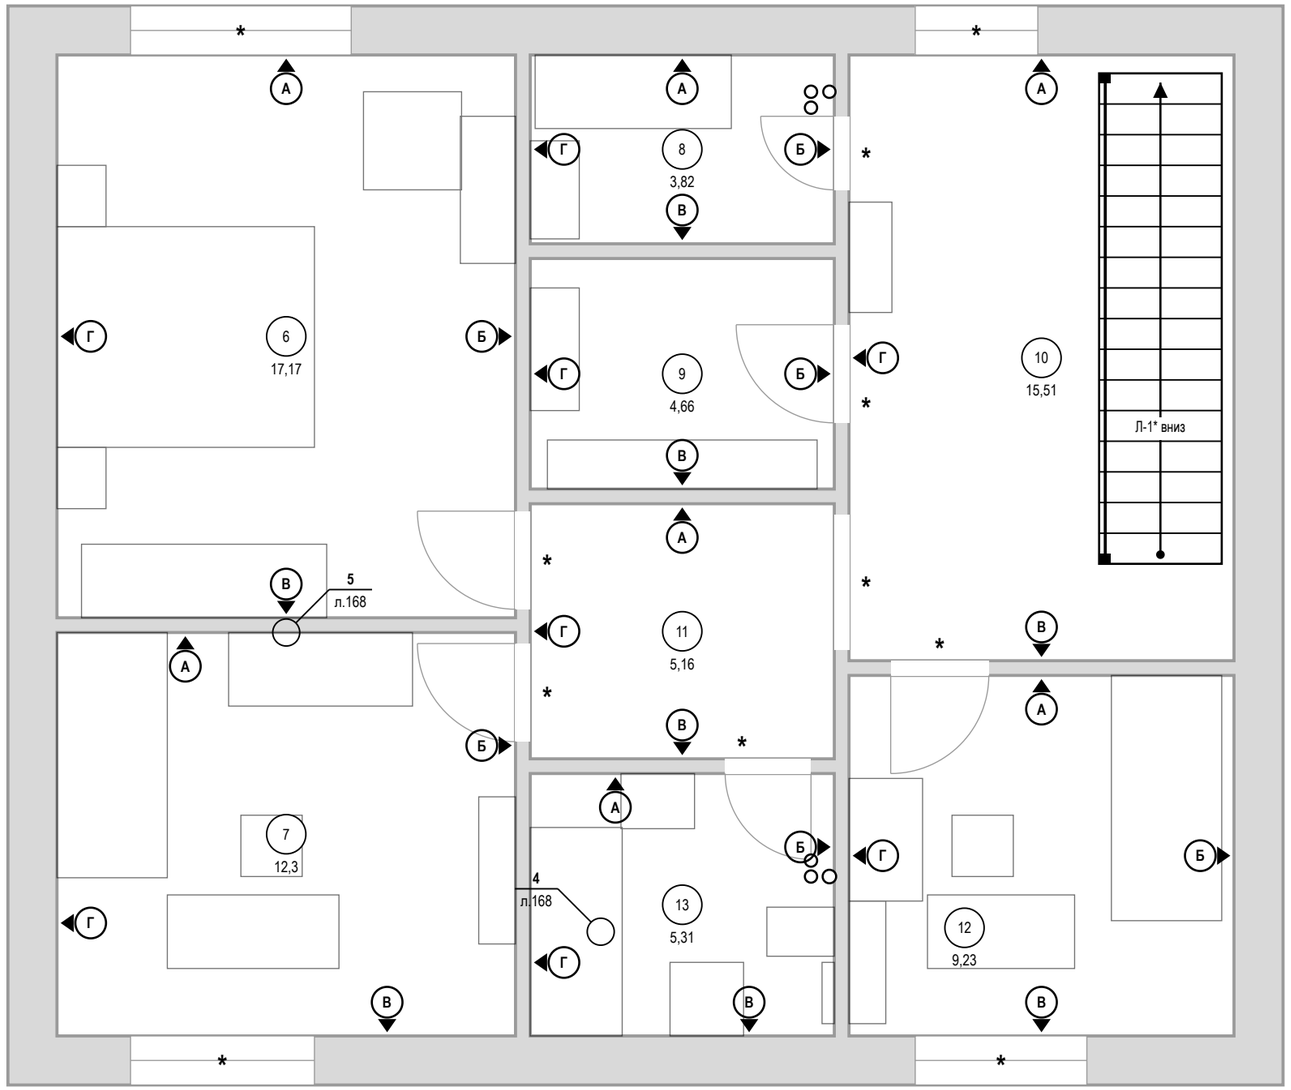

Развёртки и узлы: марка → лист

Марка	Помещение / узел	Лист
А	Спальня родителей (пом. 6)	143
Б	Спальня родителей (пом. 6)	144
В	Спальня родителей (пом. 6)	145
Г	Спальня родителей (пом. 6)	146, 147
А	Детская (пом. 7)	148
Б	Детская (пом. 7)	149
В	Детская (пом. 7)	150
Г	Детская (пом. 7)	151
А, Б	Гардеробная (пом. 8)	152
В, Г	Гардеробная (пом. 8)	153
Б, В, Г	Кладовая (пом. 9)	154
А	Холл второго этажа (пом. 10)	155
В	Холл второго этажа (пом. 10)	156
Г	Холл второго этажа (пом. 10)	157
А, В	Коридор второго этажа (пом. 11)	158
Г	Коридор второго этажа (пом. 11)	159
А	Детская вторая (пом. 12)	160
Б	Детская вторая (пом. 12)	161
В	Детская вторая (пом. 12)	162
Г	Детская вторая (пом. 12)	163
А, Б	Санузел второго этажа (пом. 13)	164, 165, 166
В, Г	Санузел второго этажа (пом. 13)	167
узел 4	Гидроизоляция санузла: заход на стены 200 мм, примыкание ванны	168
узел 5	Плинтус МДФ 80×16 мм у окрашенной стены по доске (ламинату)	168

Допущения и предложения на листе. Основа листа: взаимное расположение помещений, контур дома 9600 × 8000 и раскладка этажей подобраны проектировщиком под габариты помещений брифа; обмер и проект АР — задание (К-1); высота потолка 2900 мм — по брифу, не замерена; перекрытие 330 мм и отметка 2-го этажа +3,230 приняты; проект КР — задание (К-2); наружные стены 400 мм, перегородки 120 мм приняты (в брифе толщин нет) (К-1); разрешённая мощность 15 кВт принята по типовым ТУ для частного дома (К-4); подрайон климата не задан — принят не северный (жилые от 2,5 м) (К-7). Знак «*» — принято, не замерено (замерить): К-2: отметка чистого пола этажа «2-й этаж» +3,230; К-3: Л-1; К-5: Ст К1-1, Ст В1-1, Ст Т3-1, Ст К1-2 (кухня), Ст В1-2, Ст Т3-2. См. лист открытых вопросов (лист 7, записи К-1–К-5; лист 8, запись К-7).

Условные обозначения

- А — марка развёртки: буква стены, стрелка — взгляд
- выноска узла: над полкой — узел, под полкой — лист
- 1 — номер помещения, площадь м²

1000 мм · печать 1:1

Примечания

1. Развёртки — вид на стену изнутри помещения; буквы стен — одна система на весь альбом (как на листах выводов, плитки и отделки).
2. Стены без электроточек, мебели, декора и акцентной отделки развёрток не имеют: их отделка — по ведомости отделки помещений.
3. Узлы — на листе узлов; места применения — по выноскам этого листа и ведомости «марка → лист».

Изм.	Кол.уч	Лист	№ док.	Подп.	Дата
Разраб.		Кырлан А.С.			04.11.26
Пров.					
ГИП					
Н. контр.					
Утв.					

ГД-2026-012-АИ

Дом 120 м²

Общая площадь 147,36* м² · * размеры приняты, не замерены (реестр — л. 7–9, К-1)

Дизайн-проект интерьера

Стадия	Лист	Листов
РП	117	175

Схема расположения развёрток и узлов · 2-й этаж

М 1:50

Кырлан Александр Сергеевич


выпуск 04.11.2026 № 4dfa962484 · стр. 121 из 180

Развёртка стены А. Гостиная-кухня (пом. 1), кухонный фронт

ПРЕДВАРИТЕЛЬНО · не для производства работ · открыто пунктов: 11 (реестр — л. 7–9)

Гостиная-кухня (пом. 1) · вид изнутри помещения · размеры в мм, отметки в м от ±0,000 (чистый пол 1-го этажа)

Развёртка стены А

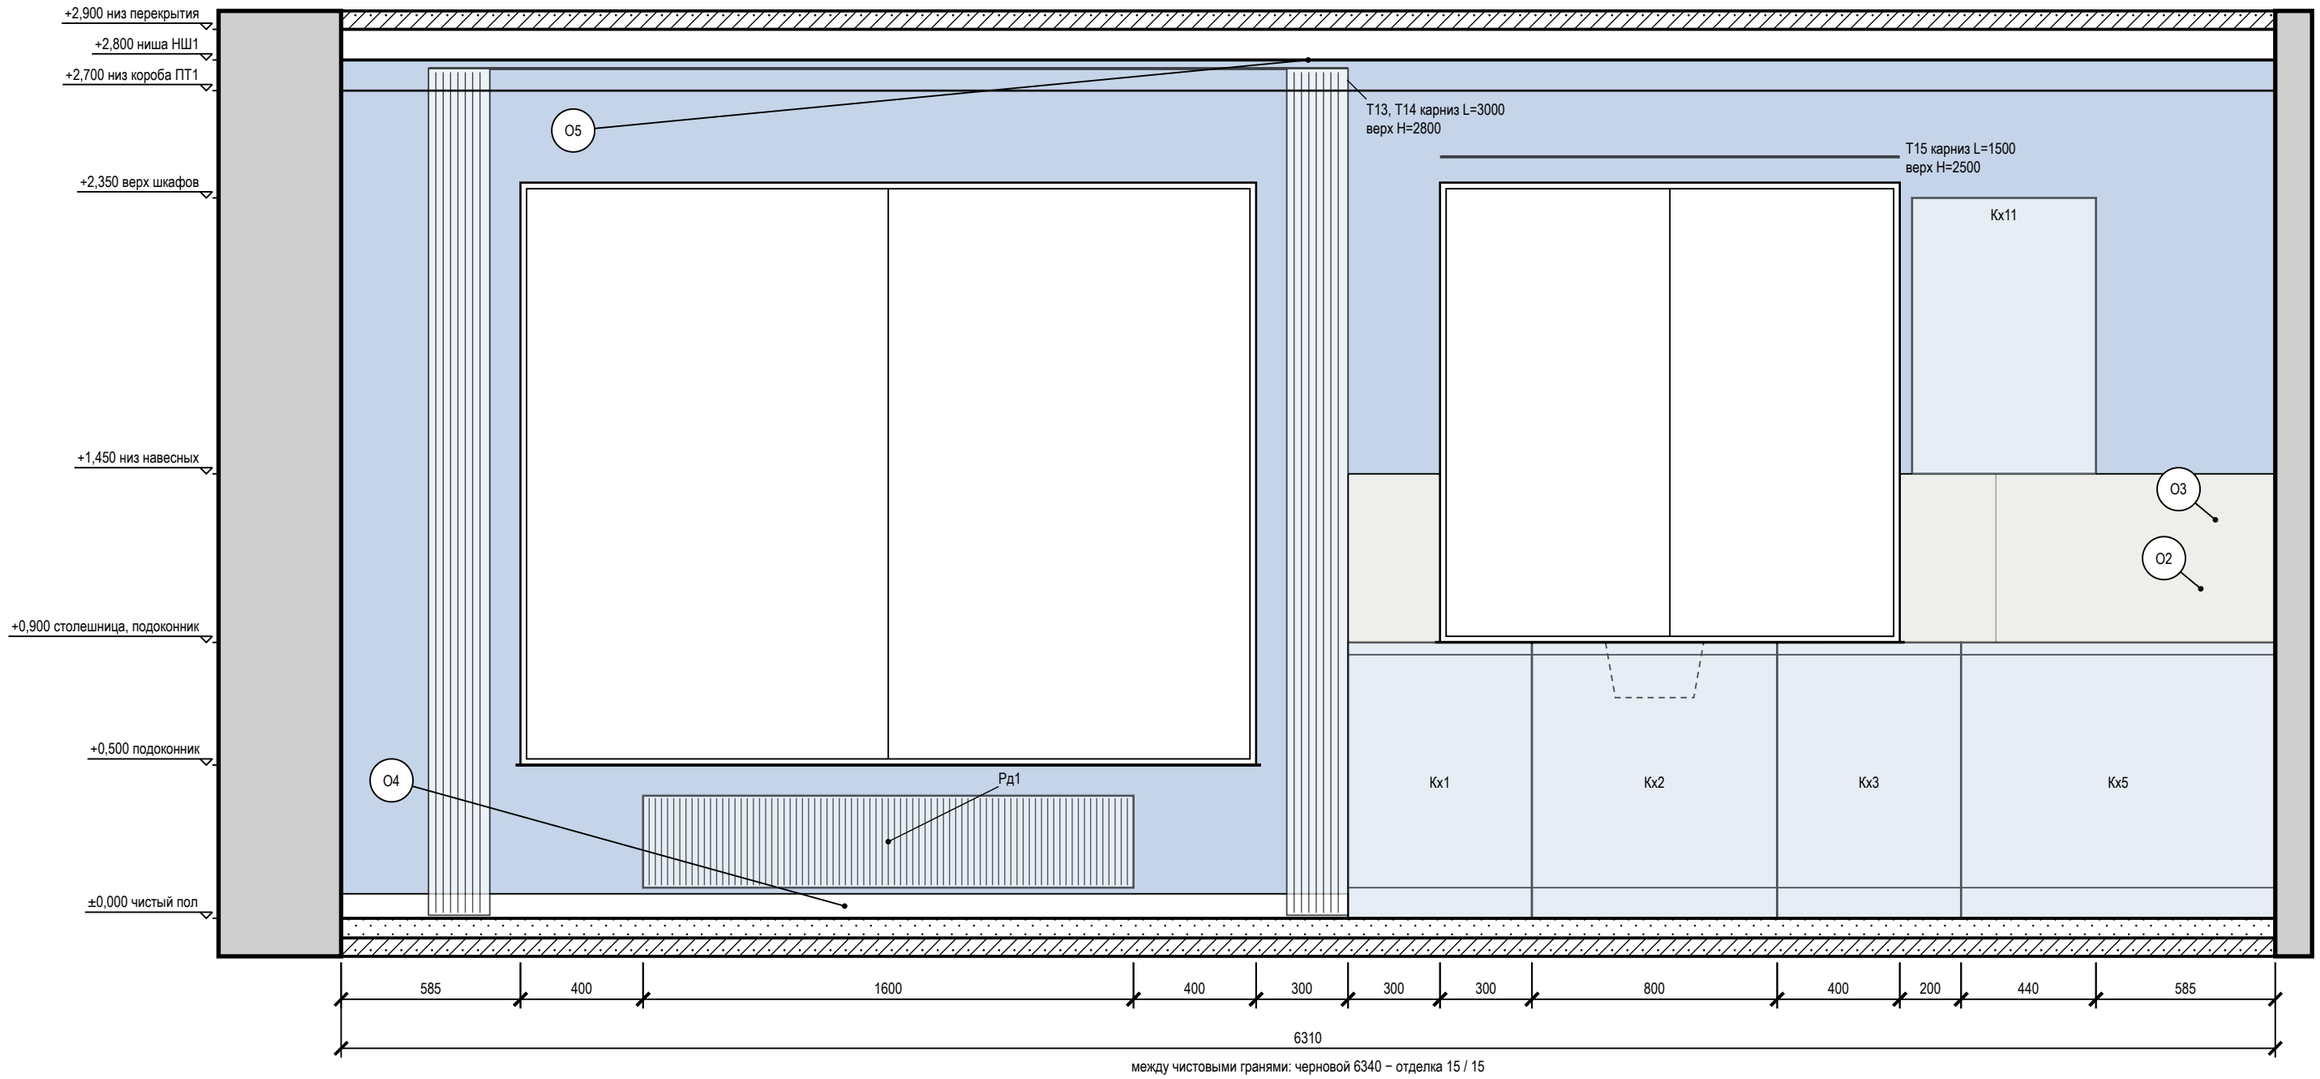

между чистовыми гранями: черновой 6340 − отделка 15 / 15

Условные обозначения

обозначения этого вида, схема развёрток помещения и ведомость отделки — на листе 120

Допущения и предложения на листе. Основа листа: взаимное расположение помещений, контур дома 9600 × 8000 и раскладка этажей подобраны проектировщиком под габариты помещений брифа; обмер и проект АР — задание (К-1); высота потолка 2900 мм — по брифу, не замерена; перекрытие 330 мм и отметка 2-го этажа +3,230 приняты; проект КР — задание (К-2); наружные стены 400 мм, перегородки 120 мм приняты (в брифе толщин нет) (К-1); разрешённая мощность 15 кВт принята по типовым ТУ для частного дома (К-4); подрайон климата не задан — принят не северный (жилые от 2,5 м) (К-7). Знак «*» — принято, не замерено (замерить): К-1: окно пом. 1 (стена А), дверь пом. 1 (стена Б). См. лист открытых вопросов (лист 7, записи К-1, К-2, К-4; лист 8, запись К-7).

Примечания

1. Развёртки — вид на стену изнутри помещения, по часовой стрелке; расположение — на схеме листа 120 и на листе 116; размеры — в мм по чистовым поверхностям; отметки — в м от ±0,000 (чистый пол 1-го этажа); высоты Н — от чистого пола помещения до оси изделия, у декора — до центра.
2. Стена А показана двумя видами: здесь — архитектурная развёртка (мебель, отделка, проёмы, высоты), электроточки и выводы ВК с привязками и таблицей — на листе 119 («Привязки»).
3. Схема мебели, приборов и декора не является технической документацией для производства мебели; габариты — по паспортам изделий.
4. Карнизы (шины) — по ведомости текстиля декоратора: длина L и верх Н на развёртке — те же числа, что в ведомости; крепление — до окраски потолка.
5. Потолок — у каждой стены свой, по плану потолков (НШ1, ПТ1); ступени — зоной, кромка короба перед нишей — тонкой линией; в поле потолка: ПТ2 +2,750, ПТ3 +2,800.

1000 мм · печать 1:1

Изм.	Кол.уч	Лист	№ док.	Подп.	Дата
Разраб.		Кырлан А.С.			04.11.26
Пров.					
ГИП					
Н. контр.					
Утв.					

ГД-2026-012-АИ

Дом 120 м²

Общая площадь 147,36* м² · * размеры приняты, не замерены (реестр — л. 7–9, К-1)

Дизайн-проект интерьера

Стадия	Лист	Листов
РП	118	175

Развёртка стены А. Гостиная-кухня (пом. 1), кухонный фронт

М 1:20

Кырлан Александр Сергеевич

выпуск 04.11.2026 № 4dfa962484 · стр. 122 из 180

Привязки электроточек и выводов ВК, стена А. Гостиная-кухня (пом. 1)

Гостиная-кухня (пом. 1) · вид изнутри помещения · привязки в мм, отметки в м · к развёртке на листе 118

ПРЕДВАРИТЕЛЬНО · не для производства работ · открыто пунктов: 11 (реестр — л. 7–9)

Развёртка стены А: электроточки и выводы

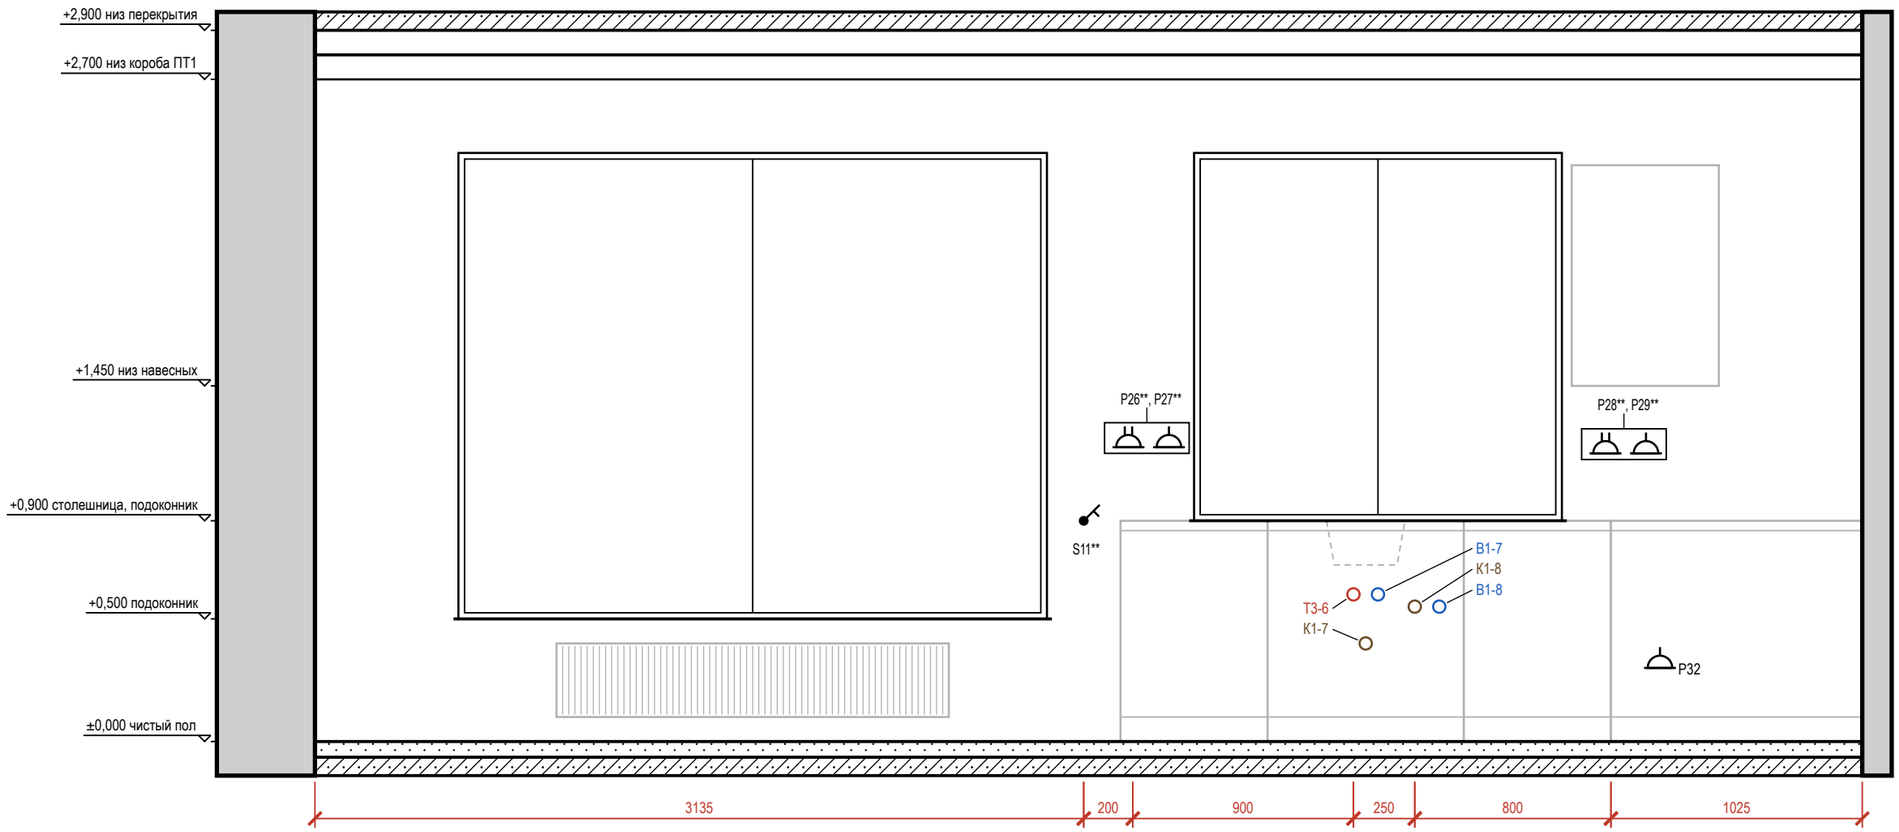


Таблица привязок электроточек и выводов

Марка	Назначение	От угла, мм	Н от пола, мм	Примечание
S11**	выключатель	3135	900	гр. 2
P26**	розетка: фартук	3335	1200	рамка 2 поста, гр. 7
P27**	розетка: фартук	3465	1200	гр. 7
T3-6	горячая вода — мойка кухонная	4235	600*	межос. 100
K1-7	канализация — мойка кухонная	4285	400*	Ø50
B1-7	холодная вода — мойка кухонная	4335	600*	межос. 100
K1-8	канализация — посудомоечная машина	4485	550*	Ø40; слив ПММ в шкафу мойки
B1-8	холодная вода — посудомоечная машина	4585	550*	кран ПММ в шкафу мойки
P28**	розетка: фартук	5285	1175	рамка 2 поста, гр. 7
P29**	розетка: фартук	5406	1175	гр. 7
P32	розетка: посудомоечная машина	5485	300	гр. 10

Условные обозначения

- розетка с заземляющим контактом; у знака — марка, ×N постов в рамке, гр. — группа щита, Н — высота оси, мм
- выключатель одноклавишный
- вывод В1 (код — в ведомости привязок)
- вывод Т3 (код — в ведомости привязок)
- вывод К1 (код — в ведомости привязок)
- привязки точек и выводов от угла и от пола, мм

Допущения и предложения на листе. Основа листа: взаимное расположение помещений, контур дома 9600 × 8000 и раскладка этажей подобраны проектировщиком под габариты помещений брифа; обмер и проект АР — задание (К-1); высота потолка 2900 мм — по брифу, не замерена; перекрытие 330 мм и отметка 2-го этажа +3,230 приняты; проект КР — задание (К-2); наружные стены 400 мм, перегородки 120 мм приняты (в брифе толщин нет) (К-1); разрешённая мощность 15 кВт принята по типовым ТУ для частного дома (К-4); подрайон климата не задан — принят не северный (жилые от 2,5 м) (К-7). Знак «*» — принято, не замерено (замерить): К-1: окно пом. 1 (стена А), дверь пом. 1 (стена Б). Знак «**» — предложено, не утверждено (согласовать): S11, P26, P27, P28, P29. См. лист открытых вопросов (лист 7, записи К-1, К-2, К-4; лист 8, запись К-7).

Примечания

1. Вид «Привязки» стены А — электроточки и выводы ВК; архитектурная развёртка (мебель, отделка, проёмы, высоты) — на листе 118, расположение — на листе 116. Мебель и приборы — подложкой для ориентира; их марки и обозначения мебели, проёмов и стен — там же.
2. Привязки — в мм: по горизонтали от левого чистового угла стены до оси изделия, Н — от чистого пола до оси; все точки — в таблице привязок. Красная цепочка — привязки по осям; точки ближе 150 мм одна к другой в цепочку не дробятся — их привязки только в таблице.
3. У знака — марка электроточки (Р — розетка, S — выключатель, Св — светильник, ЭВ — вывод кабеля); посты в рамке и группа щита — в графе «Примечание»; группы по клавишам выключателя — на листе выключателей.
4. Коды выводов ВК: В1 — холодная вода, Т3 — горячая вода, К1 — канализация; номер после дефиса — номер вывода на листе выводов сантехники; * — высота принята по типовой практике монтажа, окончательно — по паспорту прибора.
5. Выводы кухонной техники — по утверждённому проекту кухни: привязки выводов даются от осей модулей гарнитура.

1000 мм · печать 1:1

Изм.	Кол.уч	Лист	№ док.	Подп.	Дата
Разраб.		Кырлан А.С.			04.11.26
Пров.					
ГИП					
Н. контр.					
Утв.					

ГД-2026-012-АИ

Дом 120 м²

Общая площадь 147,36* м² · * размеры приняты, не замерены (реестр — л. 7–9, К-1)

Дизайн-проект интерьера

Стадия	Лист	Листов
РП	119	175

Привязки электроточек и выводов ВК, стена А. Гостиная-кухня (пом. 1)

М 1:25

Кырлан Александр Сергеевич


выпуск 04.11.2026 № 4dfa962484 · стр. 123 из 180

Развёртка стены А: схема и ведомость отделки. Гостиная-кухня (пом. 1)

Гостиная-кухня (пом. 1) · к развёртке на листе 118

ПРЕДВАРИТЕЛЬНО · не для производства работ · открыто пунктов: 11 (реестр — л. 7–9)

Схема развёрток (М 1:50)

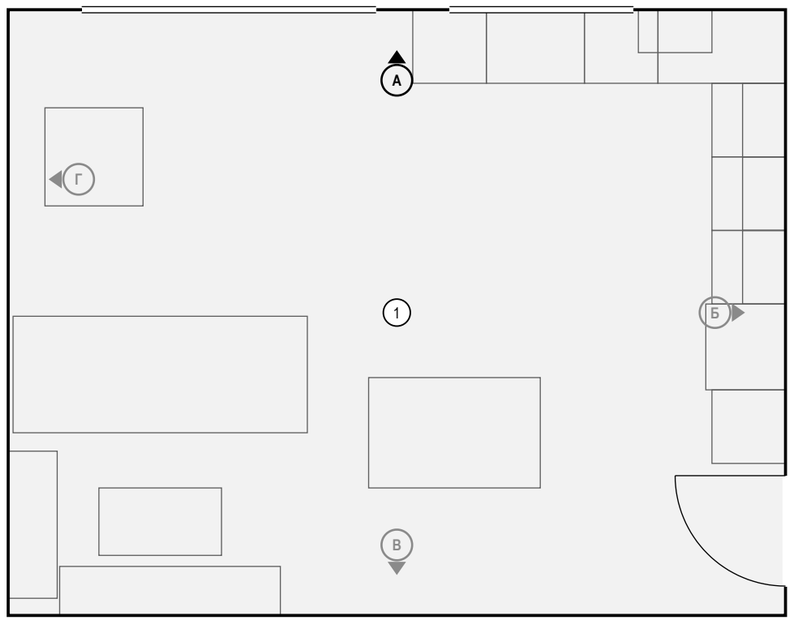

Условные обозначения

- мебель и приборы — фасад по расстановке (условно)
- карниз (шина) и шторы в собранном виде: марка Т, длина L, верх Н
- окно: проём, рама, подоконник
- радиатор отопления; марка — по плану отопления
- стены и перекрытия в сечении
- плитка: сетка швов по формату, ▲ — ось старта
- окраска: тон — цвет по коду производителя (условно)
- О1 — марка отделки по реестру отделки альбома
- А — марка развёртки: буква стены, стрелка — взгляд

Ведомость отделки (на листе)

Марка	Поверхность	Материал, изделие	Цвет, код	Кол.
О2	фартук	керамогранит, 1200×600×9 мм, аналог: керамогранит под травертин, матовый, затирка CG2WA		0,8 м²
О3	акцентная стена	окраска, Tikkurila, матовая, подготовка Q3	NCS S 3050-R80B «Эгейский синий»	9,2 м²
О4	плинтус	плинтус МДФ, h 80 мм, аналог: плинтус МДФ под покраску 80×16	Tikkurila G503 «Calla»	3,3 м
О5	потолок	окраска, Little Greene Absolute Matt, глубокоматовая, подготовка Q3	Little Greene No. 222 «Loft White»	31,3 м²

Примечания

1. Схема, условные обозначения и ведомость отделки — к развёртке стены А на листе 118: вид в своём масштабе занимает лист целиком.
2. Расположение развёрток всех помещений — на листе 116; полная ведомость отделки — на листах отделочника.

Допущения и предложения на листе

Основа листа: взаимное расположение помещений, контур дома 9600 × 8000 и раскладка этажей подобраны проектировщиком под габариты помещений брифа; обмер и проект АР — задание (К-1); высота потолка 2900 мм — по брифу, не замерена; перекрытие 330 мм и отметка 2-го этажа +3,230 приняты; проект КР — задание (К-2); наружные стены 400 мм, перегородки 120 мм приняты (в брифе толщин нет) (К-1); разрешённая мощность 15 кВт принята по типовым ТУ для частного дома (К-4); подрайон климата не задан — принят не северный (жилые от 2,5 м) (К-7).

Знак «**» — предложение проектировщика, заказчиком не утверждено (согласовать с заказчиком): плинтус пом. 1, фартук пом. 1 — артикул изделия не выбран: позиция описана характеристиками («аналог по характеристикам»), артикул выбирается при закупке.

См. лист открытых вопросов (лист 7, записи К-1, К-2, К-4; лист 8, запись К-7).

Изм.	Кол.уч	Лист	№ док.	Подп.	Дата
Разраб.		Кырлан А.С.			04.11.26
Пров.					
ГИП					
Н. контр.					
Утв.					

ГД-2026-012-АИ

Дом 120 м²

Общая площадь 147,36* м² · * размеры приняты, не замерены (реестр — л. 7–9, К-1)

Дизайн-проект интерьера

Стадия	Лист	Листов
РП	120	175

Развёртка стены А: схема и ведомость отделки. Гостиная-кухня (пом. 1)

М б/м

Кырлан Александр Сергеевич


выпуск 04.11.2026 № 4dfa962484 · стр. 124 из 180

Развёртка стены Б. Гостиная-кухня (пом. 1), кухонный фронт

Гостиная-кухня (пом. 1) · вид изнутри помещения · размеры в мм, отметки в м от ±0,000 (чистый пол 1-го этажа)


ПРЕДВАРИТЕЛЬНО · не для производства работ · открыто пунктов: 11 (реестр — л. 7–9)

Развёртка стены Б

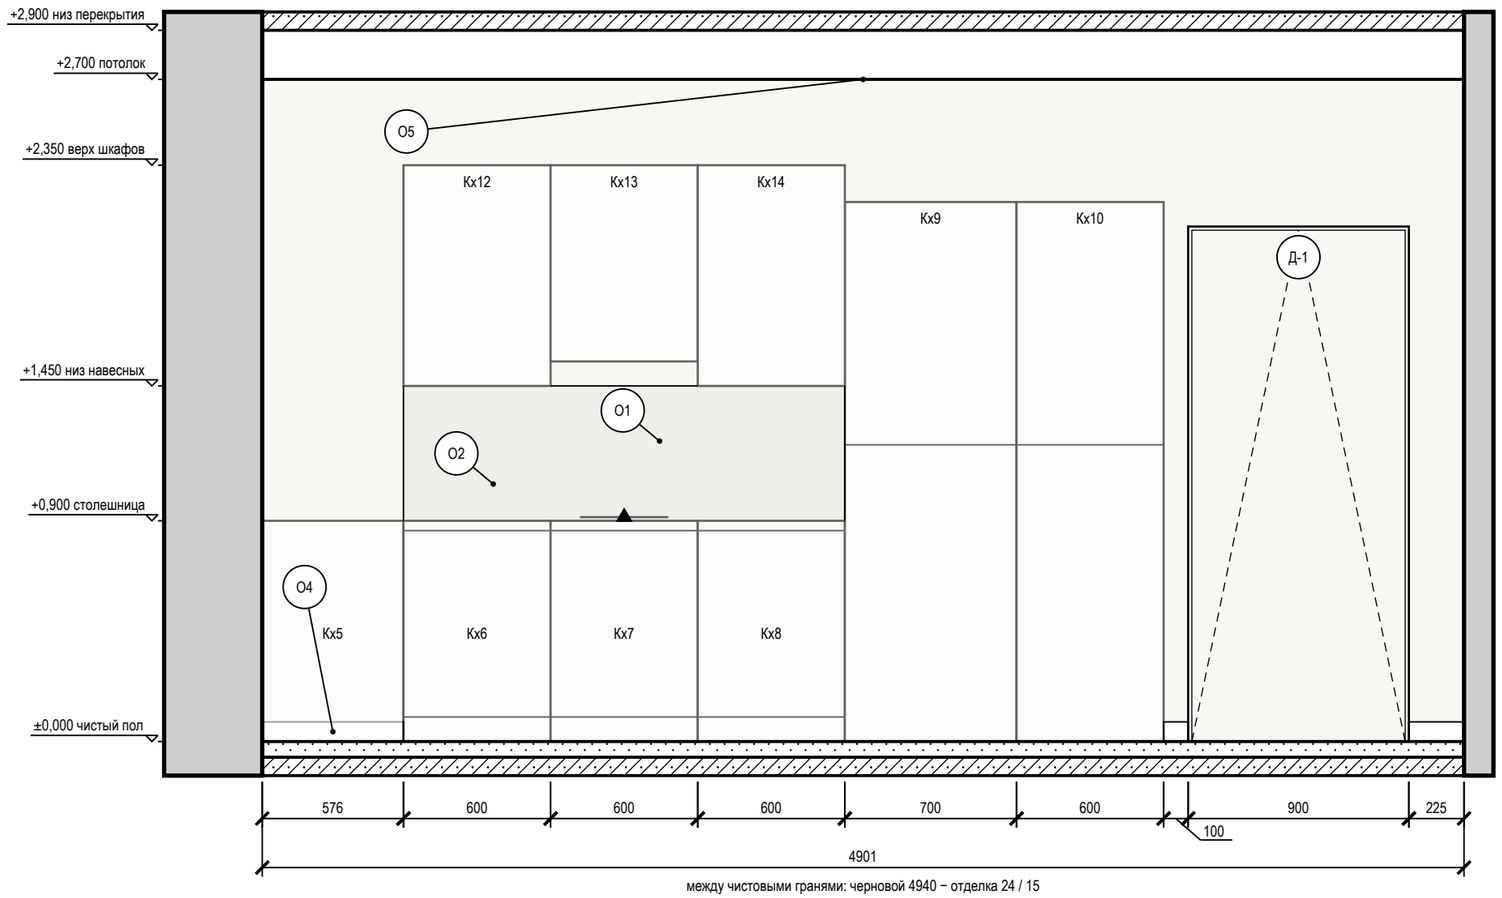

между чистовыми гранями: черновой 4940 − отделка 24 / 15

Схема развёрток (М 1:100)

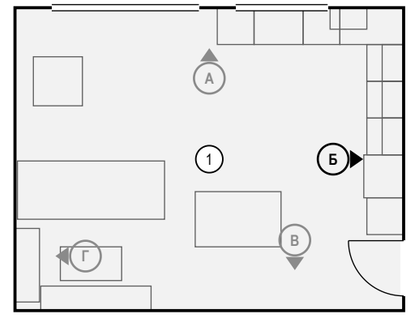

Условные обозначения

- мебель и приборы — фасад по расстановке (условно)
- дверь скрытого монтажа: полотно в плоскости стены (узел — на листе узлов)
- стены и перекрытия в сечении
- плитка: сетка швов по формату, ▲ — ось старта
- окраска: тон — цвет по коду производителя (условно)
- О1 — марка отделки по реестру отделки альбома
- А — марка развёртки: буква стены, стрелка — взгляд

Ведомость отделки (на листе)

Марка	Поверхность	Материал, изделие	Цвет, код	Кол.
О1	стены	окраска, Tikkurila, матовая, подготовка Q3	Tikkurila G503 «Calla»	10,4 м²
О2	фартук	керамогранит, 1200×600×9 мм, аналог: керамогранит под травертин, матовый, затирка CG2WA		1 м²
О4	плинтус	плинтус МДФ, h 80 мм, аналог: плинтус МДФ под покраску 80×16	Tikkurila G503 «Calla»	0,9 м
О5	потолок	окраска, Little Greene Absolute Matt, глубокоматовая, подготовка Q3	Little Greene No. 222 «Loft White»	31,3 м²

Допущения и предложения на листе

Основа листа: взаимное расположение помещений, контур дома 9600 × 8000 и раскладка этажей подобраны проектировщиком под габариты помещений брифа; обмер и проект АР — задание (К-1); высота потолка 2900 мм — по брифу, не замерена; перекрытие 330 мм и отметка 2-го этажа +3,230 приняты; проект КР — задание (К-2); наружные стены 400 мм, перегородки 120 мм приняты (в брифе толщин нет) (К-1); разрешённая мощность 15 кВт принята по типовым ТУ для частного дома (К-4); подрайон климата не задан — принят не северный (жилые от 2,5 м) (К-7).
Знак «*» — принято, не замерено и не подтверждено (замерить на объекте): К-1: окно пом. 1 (стена А) — окно: место, ширина, высота и подоконник приняты по брифу, стена — по раскладке проектировщика (К-1), не замерены; дверь пом. 1 (стена Б) — проём: место и ширина приняты проектировщиком по брифу (раскладка этажей — К-1), не замерены.
См. лист открытых вопросов (лист 7, записи К-1, К-2, К-4; лист 8, запись К-7).

Примечания

1. Развёртки — вид на стену изнутри помещения, по часовой стрелке; расположение — на схеме листа и на листе 116; размеры — в мм по чистовым поверхностям; отметки — в м от ±0,000 (чистый пол 1-го этажа); высоты Н — от чистого пола помещения до оси изделия, у декора — до центра.
2. Стена Б показана двумя видами: здесь — архитектурная развёртка (мебель, отделка, проёмы, высоты), электроточки и выводы ВК с привязками и таблицей — на листе 122 («Привязки»).
3. Схема мебели, приборов и декора не является технической документацией для производства мебели; габариты — по паспортам изделий.
4. Двери скрытого монтажа — полотно в плоскости стены, отделка стены по полотну, плинтус прерывается у короба (узел — на листе узлов).
5. Потолок — у каждой стены свой, по плану потолков (ПТ1); ступени — зоной, кромка короба перед нишей — тонкой линией; в поле потолка: ПТ2 +2,750, ПТ3 +2,800.

1000 мм · печать 1:1

Изм.	Кол.уч	Лист	№ док.	Подп.	Дата
Разраб.		Кырлан А.С.			04.11.26
Пров.					
ГИП					
Н. контр.					
Утв.					

ГД-2026-012-АИ

Дом 120 м²

Общая площадь 147,36* м² · * размеры приняты, не замерены (реестр — л. 7–9, К-1)

Дизайн-проект интерьера	Стадия	Лист	Листов
	РП	121	175

Развёртка стены Б. Гостиная-кухня (пом. 1), кухонный фронт

М 1:25

Кырлан Александр Сергеевич

выпуск 04.11.2026 № 4dfa962484 · стр. 125 из 180

Привязки электроточек, стена Б. Гостиная-кухня (пом. 1)

Гостиная-кухня (пом. 1) · вид изнутри помещения · привязки в мм, отметки в м · к развёртке на листе 121

ПРЕДВАРИТЕЛЬНО · не для производства работ · открыто пунктов: 11 (реестр — л. 7–9)

Развёртка стены Б: электроточки и выводы

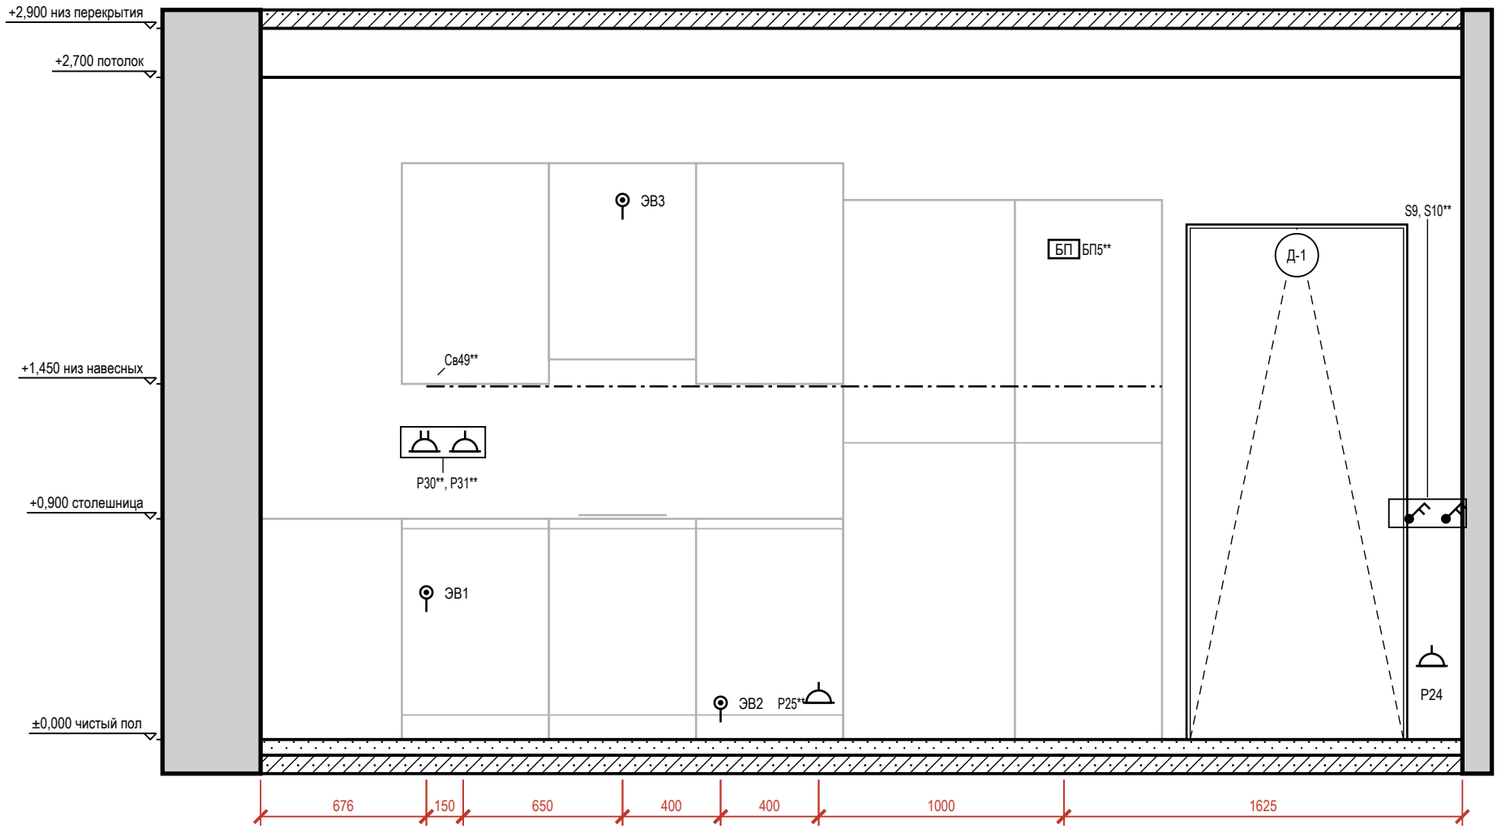


Таблица привязок электроточек и выводов

Марка	Назначение	От угла, мм	Н от пола, мм	Примечание
ЭВ1	вывод кабеля: варочная панель Кх7 (вывод в соседнем модуле Кх6, за ящиком)	676	600	гр. 8
Р30**	розетка: фартук между мойкой и варочной	676	1175	рамка 2 поста, гр. 7
Св49**	светильник настенный	676	1440	гр. 2, лента 676–3676 от угла
Р31**	розетка: фартук между мойкой и варочной	826	1175	гр. 7
ЭВ3	вывод кабеля: вытяжка	1476	2200	гр. 11
ЭВ2	вывод кабеля: духовой шкаф	1876	150	гр. 9
Р25**	розетка: холодильник Кх9 (розетка в соседнем модуле Кх8, съёмная панель)	2276	150	гр. 11
БП5**	блок питания LED: в пенале Кх10, верх, съёмная панель	3276	2000	гр. 2
Р24	розетка: у обеденного стола	4776	300	гр. 6
S9	выключатель	4776	900	гр. 2
S10**	выключатель	4856	900	рамка 2 поста, гр. 2

Условные обозначения

- розетка с заземляющим контактом; у знака — марка, ×N постов в рамке, гр. — группа щита, Н — высота оси, мм
- вывод кабеля для подключения прибора (без розетки), марка ЭВ
- выключатель одноклавишный
- выключатель двухклавишный (флажков — по числу клавиш)
- светодиодная лента в профиле / в карнизе короба
- БП — блок питания LED, с доступом (люк от 100×100 мм)
- привязки точек и выводов от угла и от пола, мм

Примечания

1. Вид «Привязки» стены Б — электроточки и выводы ВК; архитектурная развёртка (мебель, отделка, проёмы, высоты) — на листе 121, расположение — на листе 116. Мебель и приборы — подложкой для ориентира; их марки и обозначения мебели, проёмов и стен — там же.
2. Привязки — в мм: по горизонтали от левого чистового угла стены до оси изделия, Н — от чистого пола до оси; все точки — в таблице привязок. Красная цепочка — привязки по осям; точки ближе 150 мм одна к другой в цепочку не дробятся — их привязки только в таблице.
3. У знака — марка электроточки (Р — розетка, S — выключатель, Св — светильник, ЭВ — вывод кабеля); посты в рамке и группа щита — в графе «Примечание»; группы по клавишам выключателя — на листе выключателей.
4. Выводы кухонной техники — по утверждённому проекту кухни: привязки выводов даются от осей модулей гарнитура.

Допущения и предложения на листе

Основа листа: взаимное расположение помещений, контур дома 9600 × 8000 и раскладка этажей подобраны проектировщиком под габариты помещений брифа; обмер и проект АР — задание (К-1); высота потолка 2900 мм — по брифу, не замерена; перекрытие 330 мм и отметка 2-го этажа +3,230 приняты; проект КР — задание (К-2); наружные стены 400 мм, перегородки 120 мм приняты (в брифе толщин нет) (К-1); разрешённая мощность 15 кВт принята по типовым ТУ для частного дома (К-4); подрайон климата не задан — принят не северный (жилые от 2,5 м) (К-7).

Знак «*» — принято, не замерено и не подтверждено (замерить на объекте): К-1: окно пом. 1 (стена А) — окно: место, ширина, высота и подоконник приняты по брифу, стена — по раскладке проектировщика (К-1), не замерены; дверь пом. 1 (стена Б) — проём: место и ширина приняты проектировщиком по брифу (раскладка этажей — К-1), не замерены.

Знак «**» — предложение проектировщика, заказчиком не утверждено (согласовать с заказчиком): S10 — светорегулятор добавлен разработчиком проекта; Р25 — высота 2000 мм выше нормы 1 м (ПУЭ 6.6.30) по назначению: питание встроенного холодильника Кх9, розетка над нишей за съёмной панелью; Р30, Р31 — Сдвиг под раскладку плитки фартука (стена Б) на 75 мм выше — ось на шве или в центре плитки, привязка по таблице листа; Св49, БП5 — диммируемость добавлена разработчиком проекта под светорегуляторы S10 и S11. См. лист открытых вопросов (лист 7, записи К-1, К-2, К-4; лист 8, запись К-7).

1000 мм · печать 1:1

Изм.	Кол.уч	Лист	№ док.	Подп.	Дата
Разраб.		Кырлан А.С.			04.11.26
Пров.					
ГИП					
Н. контр.					
Утв.					

ГД-2026-012-АИ

Дом 120 м²

Общая площадь 147,36* м² · * размеры приняты, не замерены (реестр — л. 7–9, К-1)

Дизайн-проект интерьера

Стадия	Лист	Листов
РП	122	175

Привязки электроточек, стена Б. Гостиная-кухня (пом. 1)

М 1:25

Кырлан Александр Сергеевич


выпуск 04.11.2026 № 4dfa962484 · стр. 126 из 180

Развёртка стены В. Гостиная-кухня (пом. 1)

ПРЕДВАРИТЕЛЬНО · не для производства работ · открыто пунктов: 11 (реестр — л. 7–9)

Гостиная-кухня (пом. 1) · вид изнутри помещения · размеры в мм, отметки в м от ±0,000 (чистый пол 1-го этажа)

Развёртка стены В

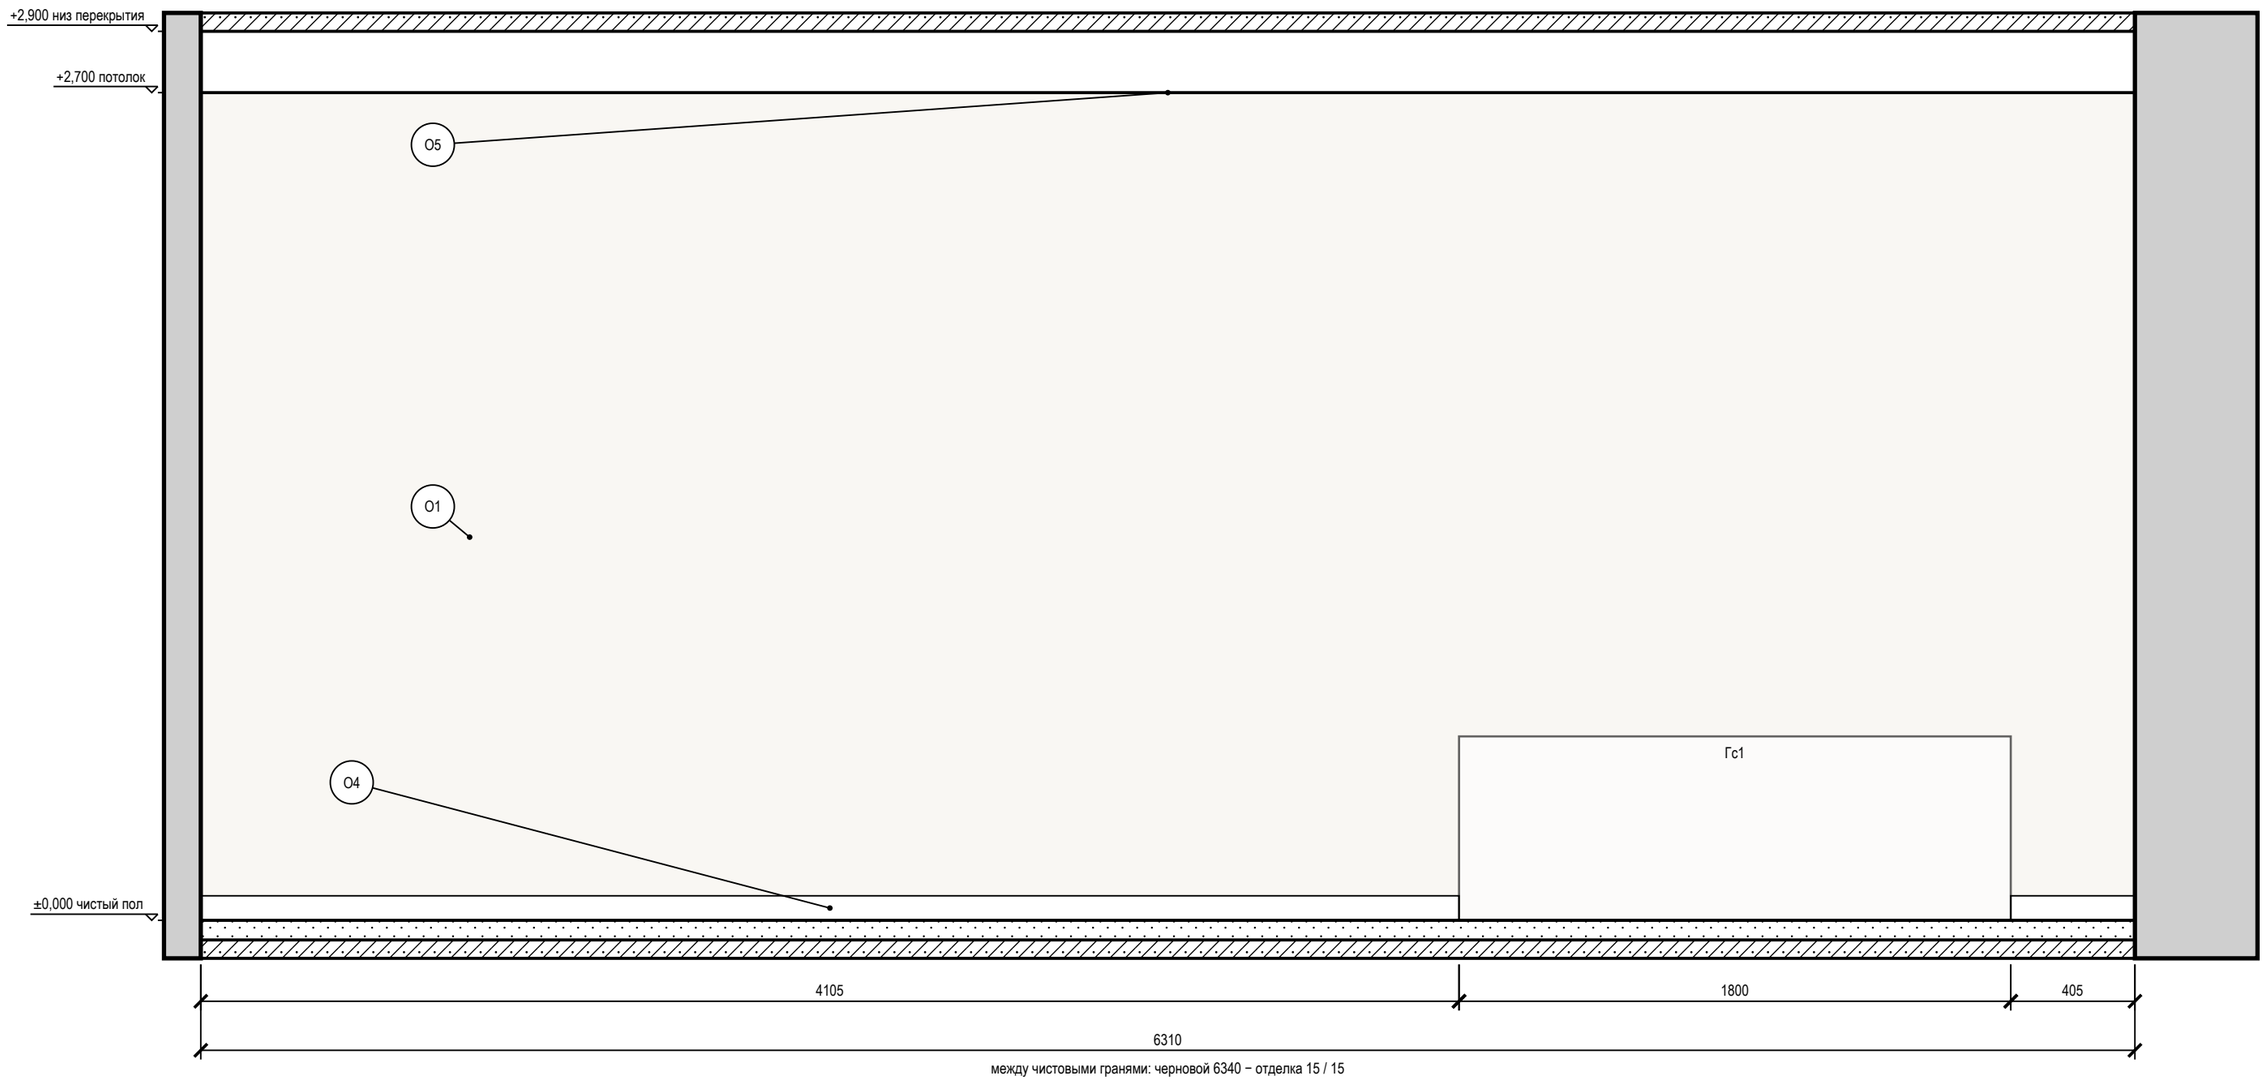

между чистовыми гранями: черновой 6340 − отделка 15 / 15

Условные обозначения

обозначения этого вида, схема развёрток помещения и ведомость отделки — на листе 125

Примечания

1. Развёртки — вид на стену изнутри помещения, по часовой стрелке; расположение — на схеме листа 125 и на листе 116; размеры — в мм по чистовым поверхностям; отметки — в м от ±0,000 (чистый пол 1-го этажа); высоты Н — от чистого пола помещения до оси изделия, у декора — до центра.
2. Стена В показана двумя видами: здесь — архитектурная развёртка (мебель, отделка, проёмы, высоты), электроточки и выводы ВК с привязками и таблицей — на листе 124 («Привязки»).
3. Схема мебели, приборов и декора не является технической документацией для производства мебели; габариты — по паспортам изделий.
4. Потолок — у каждой стены свой, по плану потолков (ПТ1); ступени — зоной, кромка короба перед нишей — тонкой линией; в поле потолка: ПТ2 +2,750, ПТ3 +2,800.

Допущения и предложения на листе. Основа листа: взаимное расположение помещений, контур дома 9600 × 8000 и раскладка этажей подобраны проектировщиком под габариты помещений брифа; обмер и проект АР — задание (К-1); высота потолка 2900 мм — по брифу, не замерена; перекрытие 330 мм и отметка 2-го этажа +3,230 приняты; проект КР — задание (К-2); наружные стены 400 мм, перегородки 120 мм приняты (в брифе толщин нет) (К-1); разрешённая мощность 15 кВт принята по типовым ТУ для частного дома (К-4); подрайон климата не задан — принят не северный (жилые от 2,5 м) (К-7). Знак «*» — принято, не замерено и не подтверждено (замерить на объекте): К-1: окно пом. 1 (стена А) — окно: место, ширина, высота и подоконник приняты по брифу, стена — по раскладке проектировщика (К-1), не замерены; дверь пом. 1 (стена Б) — проём: место и ширина приняты проектировщиком по брифу (раскладка этажей — К-1), не замерены. См. лист открытых вопросов (лист 7, записи К-1, К-2, К-4; лист 8, запись К-7).

1000 мм · печать 1:1

Изм.	Кол.уч	Лист	№ док.	Подп.	Дата
Разраб.		Кырлан А.С.			04.11.26
Пров.					
ГИП					
Н. контр.					
Утв.					

ГД-2026-012-АИ

Дом 120 м²

Общая площадь 147,36* м² · * размеры приняты, не замерены (реестр — л. 7–9, К-1)

Дизайн-проект интерьера

Стадия	Лист	Листов
РП	123	175

Развёртка стены В. Гостиная-кухня (пом. 1)

М 1:20

Кырлан Александр Сергеевич

выпуск 04.11.2026 № 4dfa962484 · стр. 127 из 180

Привязки электроточек, стена В. Гостиная-кухня (пом. 1)

Гостиная-кухня (пом. 1) · вид изнутри помещения · привязки в мм, отметки в м · к развёртке на листе 123

ПРЕДВАРИТЕЛЬНО · не для производства работ · открыто пунктов: 11 (реестр — л. 7–9)

Развёртка стены В: электроточки и выводы

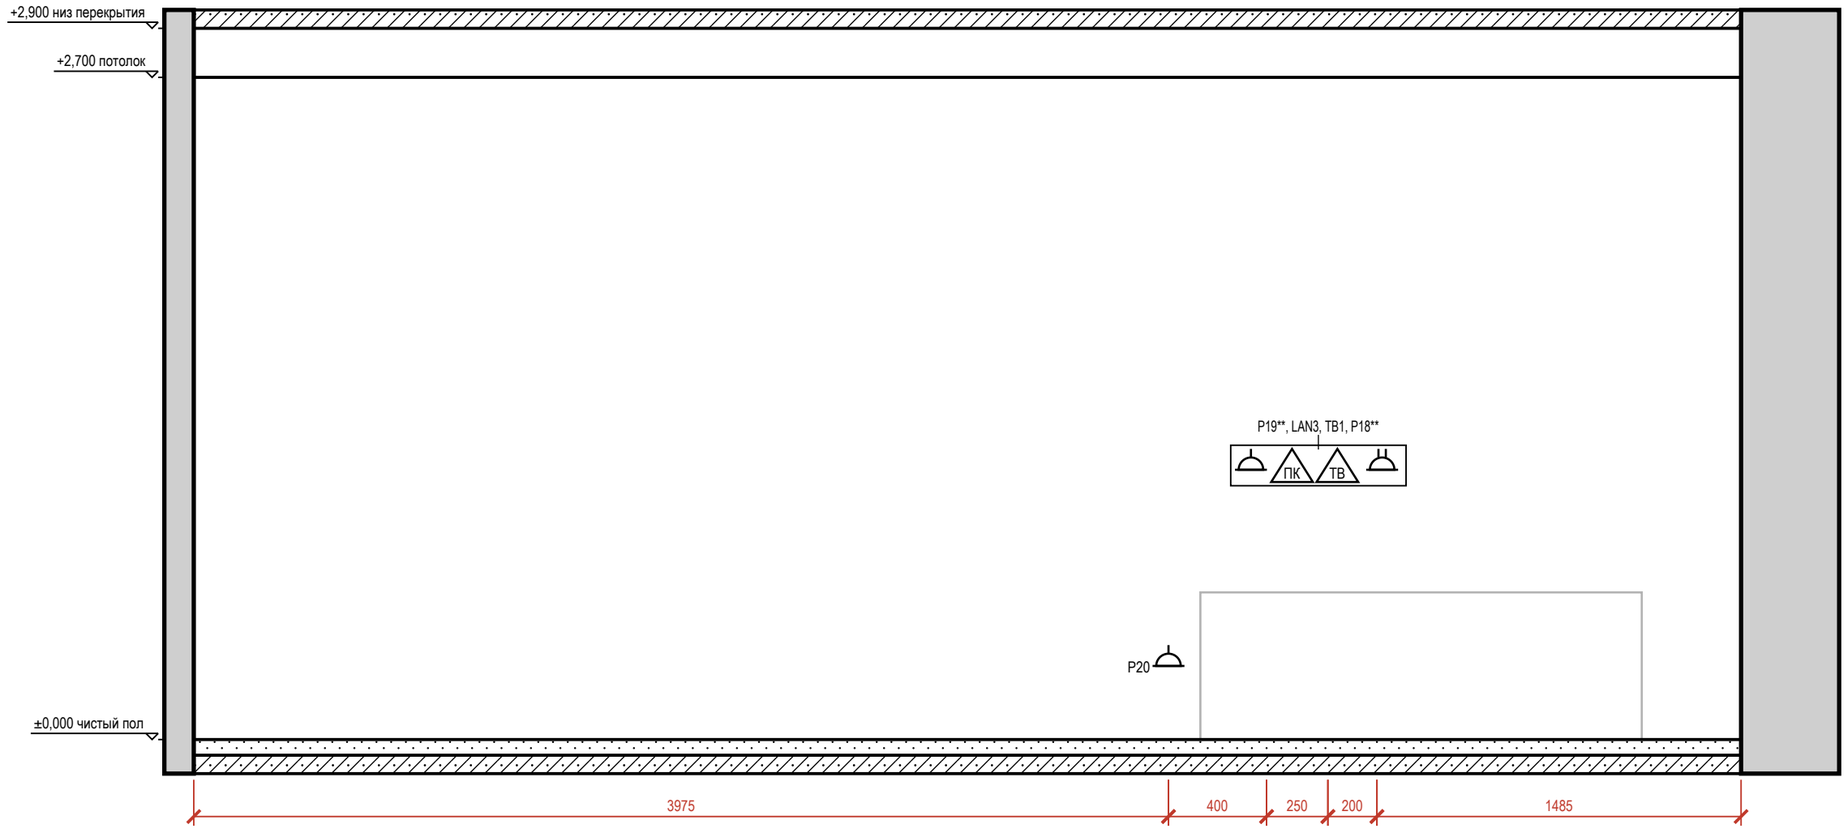


Таблица привязок электроточек и выводов

Марка	Назначение	От угла, мм	Н от пола, мм	Примечание
P20	розетка: у ТВ-тумбы	3975	300	гр. 6
P19**	розетка: ТВ-приставка (в одной зоне с TB1, LAN3)	4375	1100	гр. 6
LAN3	розетка RJ45: Smart TV	4475	1100	

Марка	Назначение	От угла, мм	Н от пола, мм	Примечание
TB1	розетка ТВ: ТВ-зона	4625	1100	
P18**	розетка: ТВ (в одной зоне с TB1, LAN3)	4825	1100	рамка 2 поста, гр. 6

Условные обозначения

- розетка с заземляющим контактом; у знака — марка, ×N постов в рамке, гр. — группа щита, Н — высота оси, мм
- ПК — розетка компьютерная RJ45
- ТВ — розетка телевизионная
- привязки точек и выводов от угла и от пола, мм

Примечания

1. Вид «Привязки» стены В — электроточки и выводы ВК; архитектурная развёртка (мебель, отделка, проёмы, высоты) — на листе 123, расположение — на листе 116. Мебель и приборы — подложкой для ориентира; их марки и обозначения мебели, проёмов и стен — там же.
2. Привязки — в мм: по горизонтали от левого чистового угла стены до оси изделия, Н — от чистого пола до оси; все точки — в таблице привязок. Красная цепочка — привязки по осям; точки ближе 150 мм одна к другой в цепочку не дробятся — их привязки только в таблице.
3. У знака — марка электроточки (Р — розетка, S — выключатель, Св — светильник, ЭВ — вывод кабеля); посты в рамке и группа щита — в графе «Примечание»; группы по клавишам выключателя — на листе выключателей.

Допущения и предложения на листе

Основа листа: взаимное расположение помещений, контур дома 9600 × 8000 и раскладка этажей подобраны проектировщиком под габариты помещений брифа; обмер и проект АР — задание (К-1); высота потолка 2900 мм — по брифу, не замерена; перекрытие 330 мм и отметка 2-го этажа +3,230 приняты; проект КР — задание (К-2); наружные стены 400 мм, перегородки 120 мм приняты (в брифе толщин нет) (К-1); разрешённая мощность 15 кВт принята по типовым ТУ для частного дома (К-4); подрайон климата не задан — принят не северный (жилые от 2,5 м) (К-7).

Знак «*» — принято, не замерено и не подтверждено (замерить на объекте): К-1: окно пом. 1 (стена А) — окно: место, ширина, высота и подоконник приняты по брифу, стена — по раскладке проектировщика (К-1), не замерены; дверь пом. 1 (стена Б) — проём: место и ширина приняты проектировщиком по брифу (раскладка этажей — К-1), не замерены.

Знак «**» — предложение проектировщика, заказчиком не утверждено (согласовать с заказчиком): P18 — высота 1100 мм выше нормы 1 м (ПУЭ 6.6.30) по назначению: питание ТВ, в одной зоне с выводами TB1 и LAN3; P19 — высота 1100 мм выше нормы 1 м (ПУЭ 6.6.30) по назначению: питание приставки ТВ, в одной зоне с выводами TB1 и LAN3.

См. лист открытых вопросов (лист 7, записи К-1, К-2, К-4; лист 8, запись К-7).

1000 мм · печать 1:1

Изм.	Кол.уч	Лист	№ док.	Подп.	Дата
Разраб.		Кырлан А.С.			04.11.26
Пров.					
ГИП					
Н. контр.					
Утв.					

ГД-2026-012-АИ

Дом 120 м²

Общая площадь 147,36* м² · * размеры приняты, не замерены (реестр — л. 7–9, К-1)

Дизайн-проект интерьера

Стадия	Лист	Листов
РП	124	175


Привязки электроточек, стена В.
Гостиная-кухня (пом. 1)
М 1:25

Кырлан Александр Сергеевич

Развёртка стены В: схема и ведомость отделки. Гостиная-кухня (пом. 1)

Гостиная-кухня (пом. 1) · к развёртке на листе 123

Схема развёрток (М 1:50)

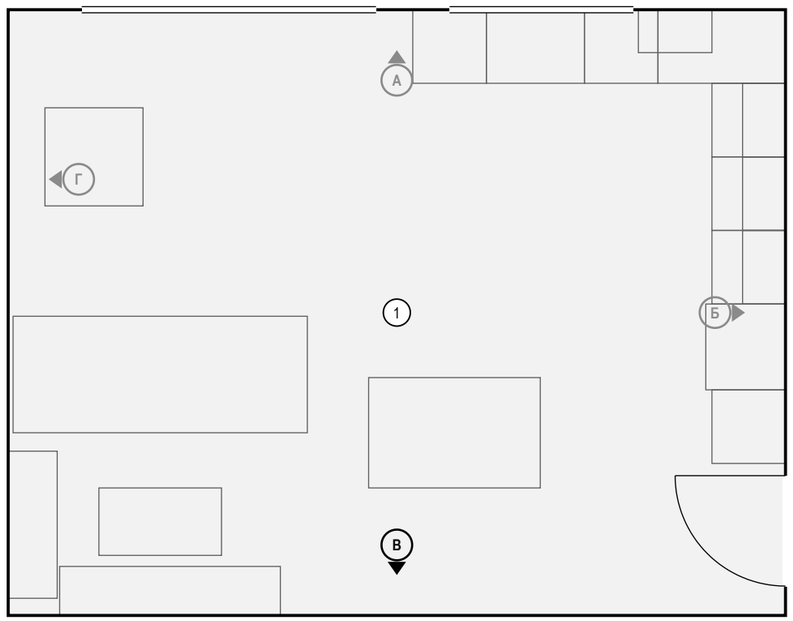

Условные обозначения

- мебель и приборы — фасад по расстановке (условно)
- стены и перекрытия в сечении
- окраска: тон — цвет по коду производителя (условно)
- О1 — марка отделки по реестру отделки альбома
- А — марка развёртки: буква стены, стрелка — взгляд

Ведомость отделки (на листе)

Марка	Поверхность	Материал, изделие	Цвет, код	Кол.
О1	стены	окраска, Tikkurila, матовая, подготовка Q3	Tikkurila G503 «Calla»	17 м²
О4	плинтус	плинтус МДФ, h 80 мм, аналог: плинтус МДФ под покраску 80×16	Tikkurila G503 «Calla»	4,5 м
О5	потолок	окраска, Little Greene Absolute Matt, глубокоматовая, подготовка Q3	Little Greene No. 222 «Loft White»	31,3 м²

Примечания

1. Схема, условные обозначения и ведомость отделки — к развёртке стены В на листе 123: вид в своём масштабе занимает лист целиком.
2. Расположение развёрток всех помещений — на листе 116; полная ведомость отделки — на листах отделочника.

Допущения и предложения на листе

Основа листа: взаимное расположение помещений, контур дома 9600 × 8000 и раскладка этажей подобраны проектировщиком под габариты помещений брифа; обмер и проект АР — задание (К-1); высота потолка 2900 мм — по брифу, не замерена; перекрытие 330 мм и отметка 2-го этажа +3,230 приняты; проект КР — задание (К-2); наружные стены 400 мм, перегородки 120 мм приняты (в брифе толщин нет) (К-1); разрешённая мощность 15 кВт принята по типовым ТУ для частного дома (К-4); подрайон климата не задан — принят не северный (жилые от 2,5 м) (К-7).

Знак «**» — предложение проектировщика, заказчиком не утверждено (согласовать с заказчиком): плинтус пом. 1, фартук пом. 1 — артикул изделия не выбран: позиция описана характеристиками («аналог по характеристикам»), артикул выбирается при закупке.

См. лист открытых вопросов (лист 7, записи К-1, К-2, К-4; лист 8, запись К-7).

Изм.	Кол.уч	Лист	№ док.	Подп.	Дата
Разраб.		Кырлан А.С.			04.11.26
Пров.					
ГИП					
Н. контр.					
Утв.					

ГД-2026-012-АИ

Дом 120 м²

Общая площадь 147,36* м² · * размеры приняты, не замерены (реестр — л. 7–9, К-1)

Дизайн-проект интерьера

Стадия	Лист	Листов
РП	125	175

Развёртка стены В: схема и ведомость отделки. Гостиная-кухня (пом. 1)

М б/м


Кырлан Александр Сергеевич

Развёртка стены Г. Гостиная-кухня (пом. 1)

Гостиная-кухня (пом. 1) · вид изнутри помещения · размеры в мм, отметки в м от ±0,000 (чистый пол 1-го этажа)


ПРЕДВАРИТЕЛЬНО · не для производства работ · открыто пунктов: 11 (реестр — л. 7–9)

Развёртка стены Г

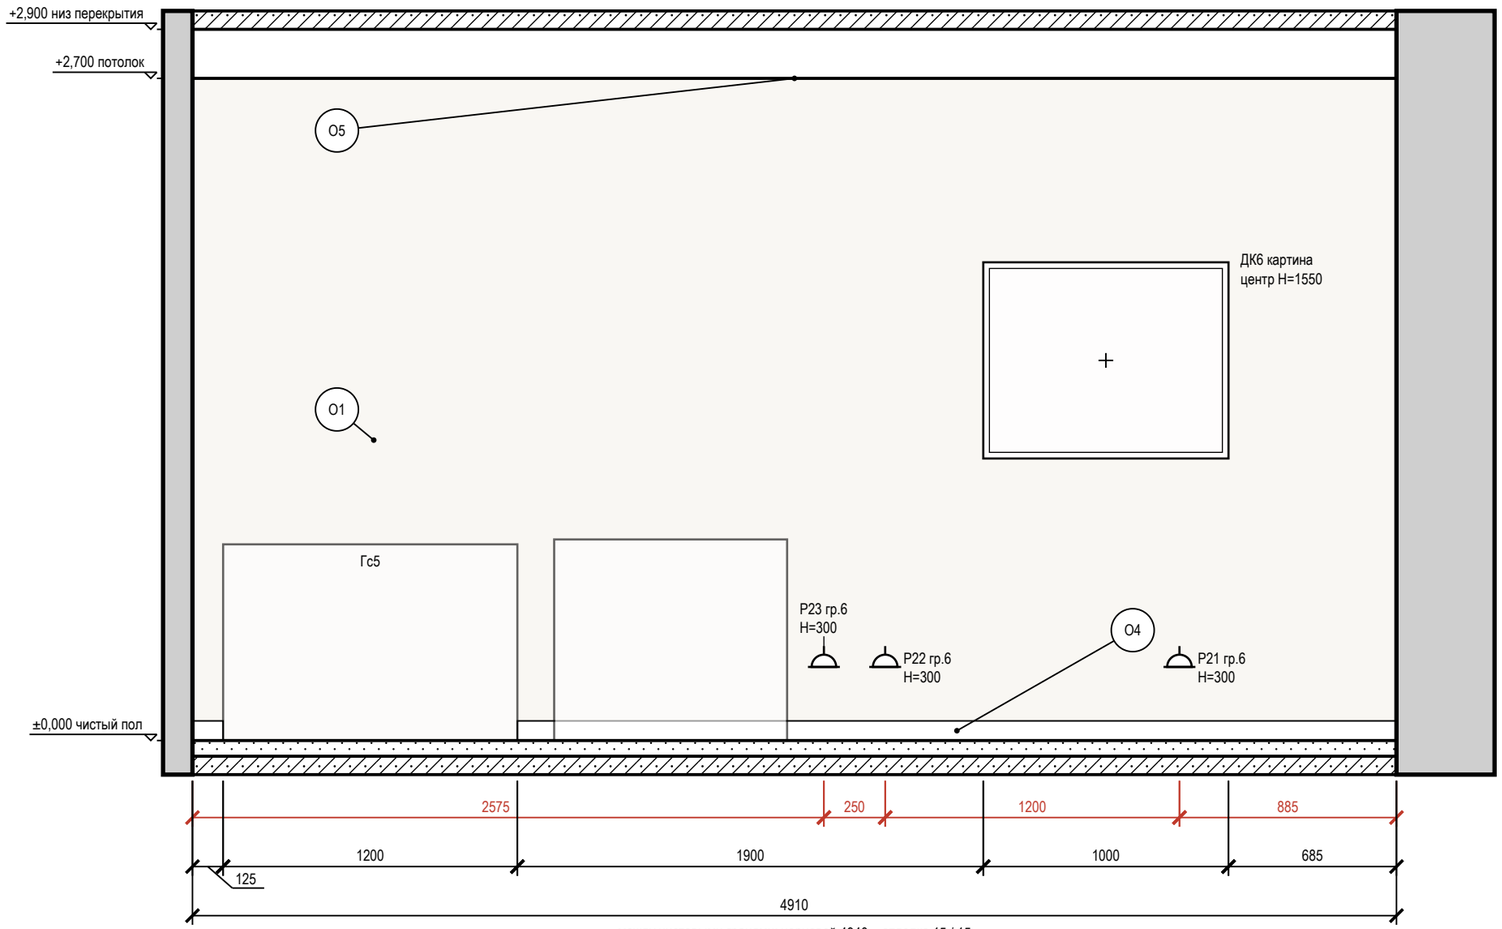

между чистовыми гранями: черновой 4940 − отделка 15 / 15

Схема развёрток (М 1:100)

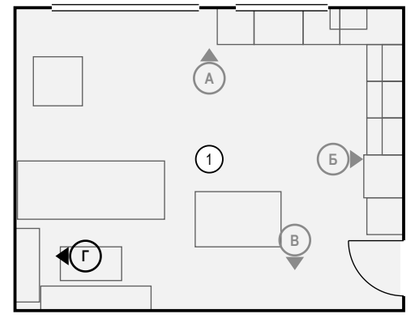

Условные обозначения

- розетка с заземляющим контактом; у знака — марка, ×N постов в рамке, гр. — группа щита, Н — высота оси, мм
- привязки точек и выводов от угла и от пола, мм
- мебель и приборы — фасад по расстановке (условно)
- картина (декор): марка Д, крест — центр, Н — высота центра, мм
- стены и перекрытия в сечении
- окраска: тон — цвет по коду производителя (условно)
- О1 — марка отделки по реестру отделки альбома
- А — марка развёртки: буква стены, стрелка — взгляд

Ведомость отделки (на листе)

Марка	Поверхность	Материал, изделие	Цвет, код	Кол.
О1	стены	окраска, Tikkurila, матовая, подготовка Q3	Tikkurila G503 «Calla»	13,3 м²
О4	плинтус	плинтус МДФ, h 80 мм, аналог: плинтус МДФ под покраску 80×16	Tikkurila G503 «Calla»	3,7 м
О5	потолок	окраска, Little Greene Absolute Matt, глубокоматовая, подготовка Q3	Little Greene No. 222 «Loft White»	31,3 м²

Допущения и предложения на листе

Основа листа: взаимное расположение помещений, контур дома 9600 × 8000 и раскладка этажей подобраны проектировщиком под габариты помещений брифа; обмер и проект АР — задание (К-1); высота потолка 2900 мм — по брифу, не замерена; перекрытие 330 мм и отметка 2-го этажа +3,230 приняты; проект КР — задание (К-2); наружные стены 400 мм, перегородки 120 мм приняты (в брифе толщин нет) (К-1); разрешённая мощность 15 кВт принята по типовым ТУ для частного дома (К-4); подрайон климата не задан — принят не северный (жилые от 2,5 м) (К-7).
Знак «*» — принято, не замерено и не подтверждено (замерить на объекте): К-1: окно пом. 1 (стена А) — окно: место, ширина, высота и подоконник приняты по брифу, стена — по раскладке проектировщика (К-1), не замерены; дверь пом. 1 (стена Б) — проём: место и ширина приняты проектировщиком по брифу (раскладка этажей — К-1), не замерены.
См. лист открытых вопросов (лист 7, записи К-1, К-2, К-4; лист 8, запись К-7).

Примечания

1. Развёртки — вид на стену изнутри помещения, по часовой стрелке; расположение — на схеме листа и на листе 116; размеры — в мм по чистовым поверхностям; отметки — в м от ±0,000 (чистый пол 1-го этажа); высоты Н — от чистого пола помещения до оси изделия, у декора — до центра.
2. Красная цепочка — привязки электроточек и выводов по осям от угла чистовых стен; высота Н — у знака, от чистого пола до оси; высоты мебели, проёмов и границ отделки — колонкой отметок слева. Стена с 5 и более точками или с мелкими звеньями привязок показана двумя видами: архитектурная развёртка (мебель, отделка, проёмы, высоты) и вид «Привязки» на отдельном листе — точки и выводы с марками, одна цепочка по осям и таблица привязок (каждая точка — строка).
3. У знака электроточки: марка (Р — розетка, S — выключатель, Св — светильник, ЭВ — вывод кабеля), ×N — число постов в рамке, гр. — группа щита, Н — высота оси от чистого пола, мм; группы по клавишам выключателя — на листе выключателей.
4. Схема мебели, приборов и декора не является технической документацией для производства мебели; габариты — по паспортам изделий.
5. Картины и зеркала крепить к основанию по паспорту изделия (закладные и анкеры — в перечне скрытых работ); крест — ось центра предмета.
6. Потолок — у каждой стены свой, по плану потолков (ПТ1); ступени — зоной, кромка короба перед нишей — тонкой линией; в поле потолка: ПТ2 +2,750, ПТ3 +2,800.

1000 мм · печать 1:1

Изм.	Кол.уч	Лист	№ док.	Подп.	Дата
Разраб.		Кырлан А.С.			04.11.26
Пров.					
ГИП					
Н. контр.					
Утв.					

ГД-2026-012-АИ

Дом 120 м²

Общая площадь 147,36* м² · * размеры приняты, не замерены (реестр — л. 7–9, К-1)

Дизайн-проект интерьера	Стадия	Лист	Листов
	РП	126	175

Развёртка стены Г. Гостиная-кухня (пом. 1)

М 1:25

Кырлан Александр Сергеевич


выпуск 04.11.2026 № 4dfa962484 · стр. 130 из 180

Развёртка стены А. Холл с лестницей (пом. 2)

Холл с лестницей (пом. 2) · вид изнутри помещения · размеры в мм, отметки в м от ±0,000 (чистый пол 1-го этажа)


ПРЕДВАРИТЕЛЬНО · не для производства работ · открыто пунктов: 11 (реестр — л. 7–9)

Развёртка стены А

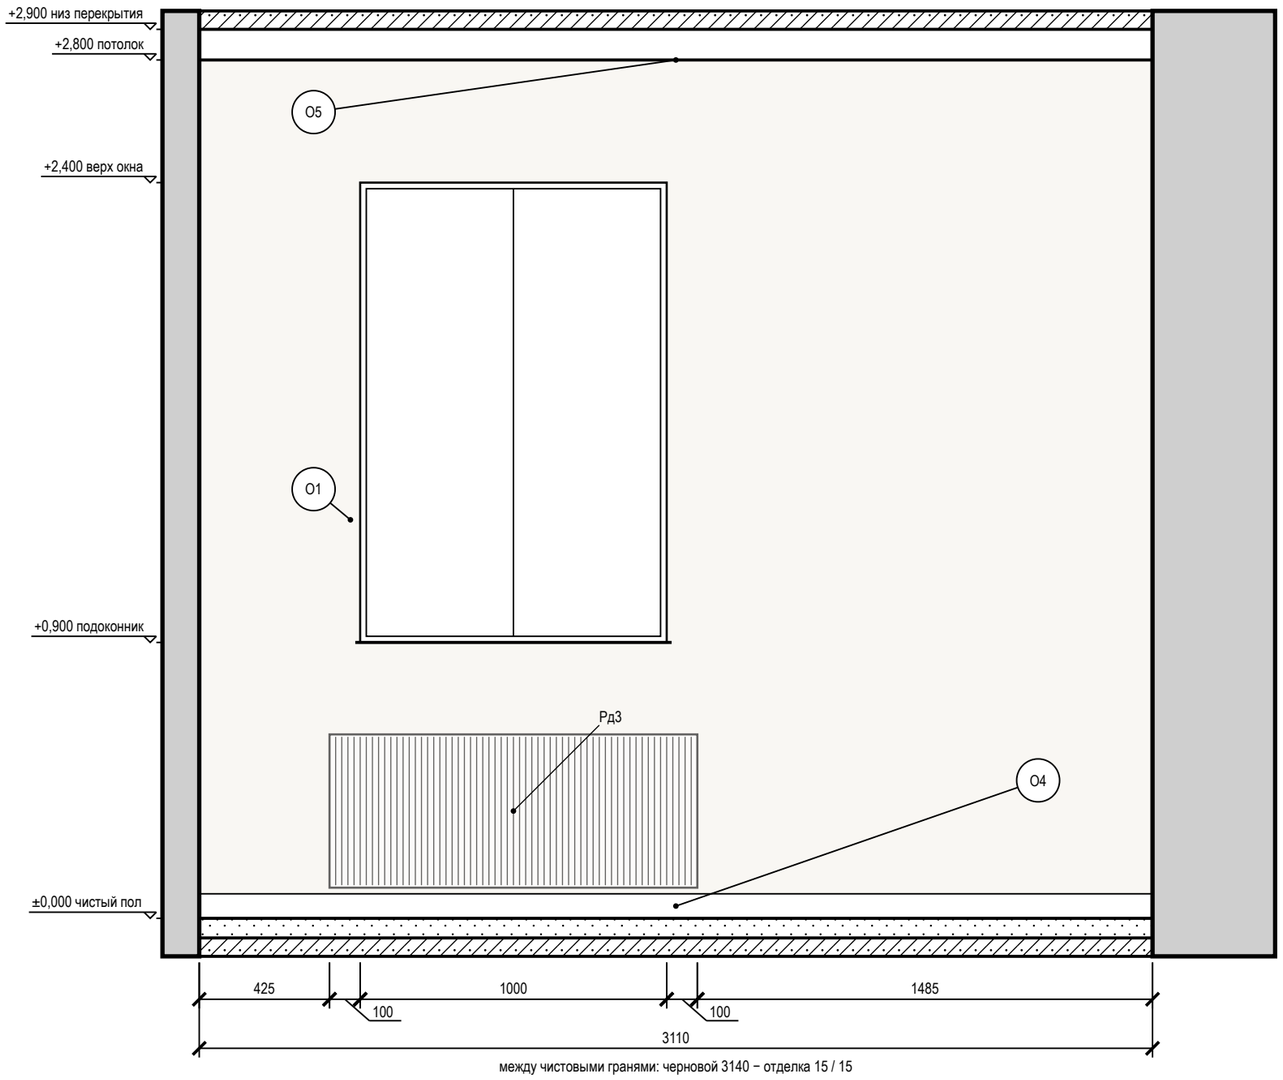

между чистовыми гранями: черновой 3140 − отделка 15 / 15

Схема развёрток (М 1:100)

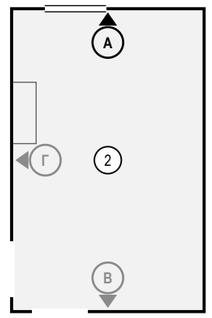

Допущения и предложения на листе

Основа листа: взаимное расположение помещений, контур дома 9600 × 8000 и раскладка этажей подобраны проектировщиком под габариты помещений брифа; обмер и проект АР — задание (К-1); высота потолка 2900 мм — по брифу, не замерена; перекрытие 330 мм и отметка 2-го этажа +3,230 приняты; проект КР — задание (К-2); наружные стены 400 мм, перегородки 120 мм приняты (в брифе толщин нет) (К-1); разрешённая мощность 15 кВт принята по типовым ТУ для частного дома (К-4); подрайон климата не задан — принят не северный (жилые от 2,5 м) (К-7).

Знак «*» — принято, не замерено и не подтверждено (замерить на объекте): К-1: окно пом. 2 (стена А) — окно: место, ширина, высота и подоконник приняты по брифу, стена — по раскладке проектировщика (К-1), не замерены.

Изменения по листу без подписи: ИЗ-2.

См. лист открытых вопросов (лист 7, записи К-1, К-2, К-4; лист 8, запись К-7; лист 9, запись ИЗ-2).

Условные обозначения

- мебель и приборы — фасад по расстановке (условно)
- окно: проём, рама, подоконник
- радиатор отопления; марка — по плану отопления
- стены и перекрытия в сечении
- окраска: тон — цвет по коду производителя (условно)
- О1 — марка отделки по реестру отделки альбома
- А — марка развёртки: буква стены, стрелка — взгляд

Ведомость отделки (на листе)

Марка	Поверхность	Материал, изделие	Цвет, код	Кол.
О1	стены	окраска, Tikkurila, матовая, подготовка Q3	Tikkurila G503 «Calla»	7,2 м²
О4	плинтус	плинтус МДФ, h 80 мм, аналог: плинтус МДФ под покраску 80×16	Tikkurila G503 «Calla»	3,1 м
О5	потолок	окраска, Little Greene Absolute Matt, глубокоматовая, подготовка Q3	Little Greene No. 222 «Loft White»	15,5 м²

Примечания

1. Развёртки — вид на стену изнутри помещения, по часовой стрелке; расположение — на схеме листа и на листе 116; размеры — в мм по чистовым поверхностям; отметки — в м от ±0,000 (чистый пол 1-го этажа); высоты Н — от чистого пола помещения до оси изделия, у декора — до центра.
2. Схема мебели, приборов и декора не является технической документацией для производства мебели; габариты — по паспортам изделий.

1000 мм · печать 1:1

Изм.	Кол.уч	Лист	№ док.	Подп.	Дата
Разраб.		Кырлан А.С.			04.11.26
Пров.					
ГИП					
Н. контр.					
Утв.					

ГД-2026-012-АИ

Дом 120 м²

Общая площадь 147,36* м² · * размеры приняты, не замерены (реестр — л. 7–9, К-1)

Дизайн-проект интерьера

Стадия	Лист	Листов
РП	127	175

Развёртка стены А. Холл с лестницей (пом. 2)

М 1:20


Кырлан Александр Сергеевич

выпуск 04.11.2026 № 4dfa962484 · стр. 131 из 180

Развёртка стены В. Холл с лестницей (пом. 2)


Холл с лестницей (пом. 2) · вид изнутри помещения · размеры в мм, отметки в м от ±0,000 (чистый пол 1-го этажа)

Развёртка стены В

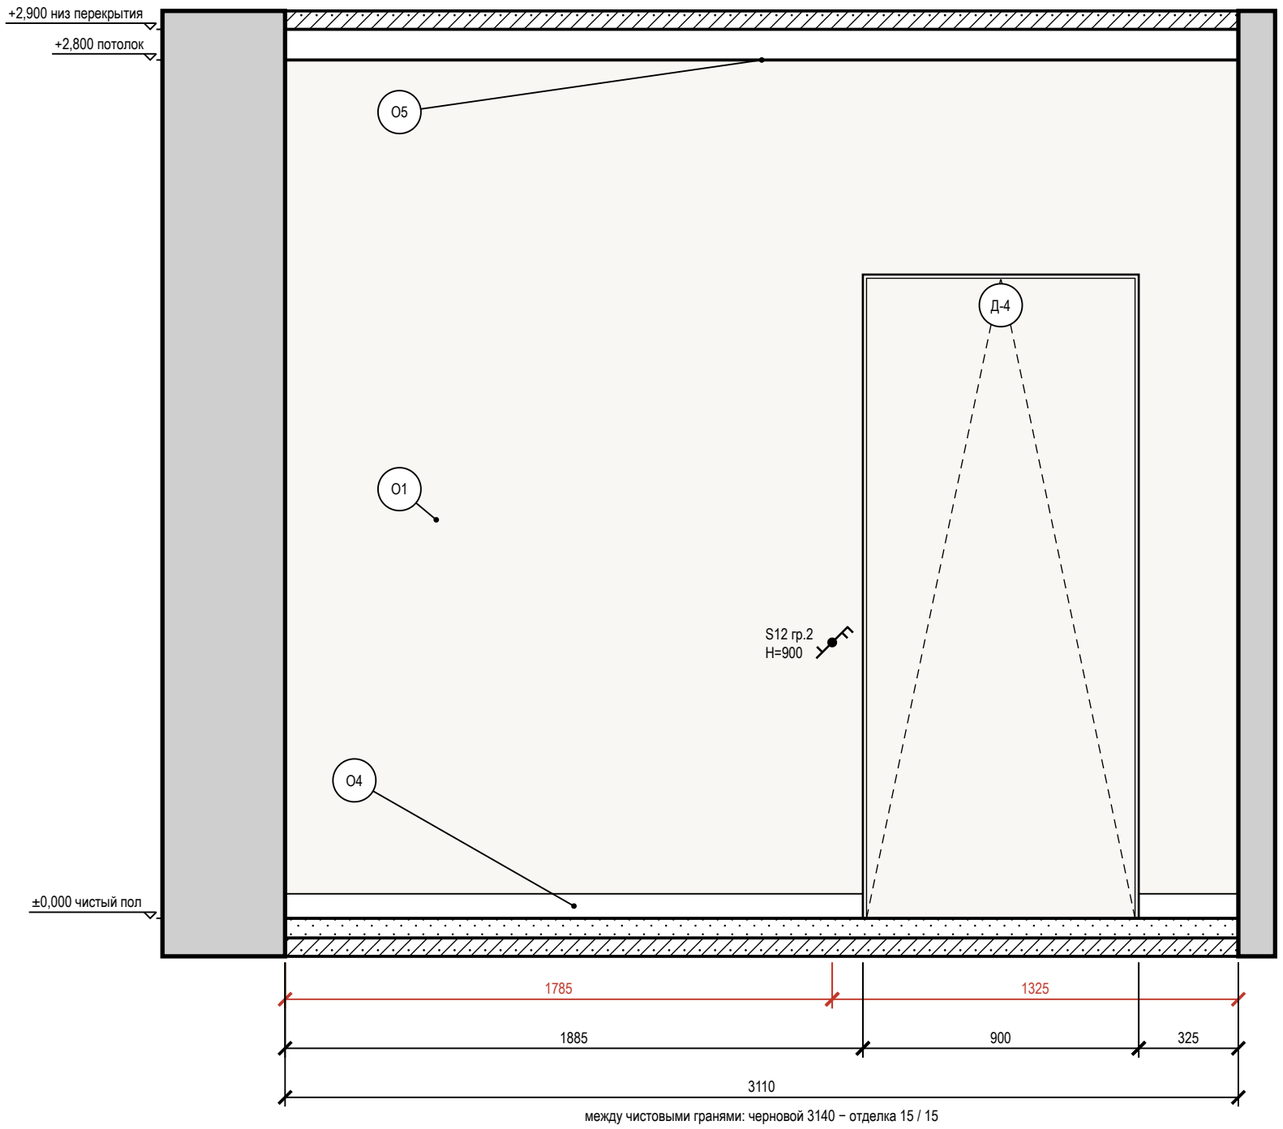

между чистовыми гранями: черновой 3140 − отделка 15 / 15

Схема развёрток (М 1:100)

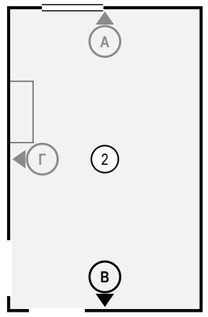

Допущения и предложения на листе

Основа листа: взаимное расположение помещений, контур дома 9600 × 8000 и раскладка этажей подобраны проектировщиком под габариты помещений брифа; обмер и проект АР — задание (К-1); высота потолка 2900 мм — по брифу, не замерена; перекрытие 330 мм и отметка 2-го этажа +3,230 приняты; проект КР — задание (К-2); наружные стены 400 мм, перегородки 120 мм приняты (в брифе толщин нет) (К-1); разрешённая мощность 15 кВт принята по типовым ТУ для частного дома (К-4); подрайон климата не задан — принят не северный (жилые от 2,5 м) (К-7).

Знак «*» — принято, не замерено и не подтверждено (замерить на объекте): К-1: окно пом. 2 (стена А) — окно: место, ширина, высота и подоконник приняты по брифу, стена — по раскладке проектировщика (К-1), не замерены. См. лист открытых вопросов (лист 7, записи К-1, К-2, К-4; лист 8, запись К-7).

Условные обозначения

- выключатель одноклавишный
- выключатель двухклавишный (флажков — по числу клавиш)
- выключатель с проходной или перекрёстной клавишей (обратный флажок); тип клавиши — в подписи
- привязки точек и выводов от угла и от пола, мм
- мебель и приборы — фасад по расстановке (условно)
- дверь скрытого монтажа: полотно в плоскости стены (узел — на листе узлов)
- стены и перекрытия в сечении
- окраска: тон — цвет по коду производителя (условно)
- О1 — марка отделки по реестру отделки альбома
- А — марка развёртки: буква стены, стрелка — взгляд

Ведомость отделки (на листе)

Марка	Поверхность	Материал, изделие	Цвет, код	Кол.
О1	стены	окраска, Tikkurila, матовая, подготовка Q3	Tikkurila G503 «Calla»	6,8 м²
О4	плинтус	плинтус МДФ, h 80 мм, аналог: плинтус МДФ под покраску 80×16	Tikkurila G503 «Calla»	2,2 м
О5	потолок	окраска, Little Greene Absolute Matt, глубокоматовая, подготовка Q3	Little Greene No. 222 «Loft White»	15,5 м²

Примечания

1. Развёртки — вид на стену изнутри помещения, по часовой стрелке; расположение — на схеме листа и на листе 116; размеры — в мм по чистовым поверхностям; отметки — в м от ±0,000 (чистый пол 1-го этажа); высоты Н — от чистого пола помещения до оси изделия, у декора — до центра.
2. Красная цепочка — привязки электроточек и выводов по осям от угла чистовых стен; высота Н — у знака, от чистого пола до оси; высоты мебели, проёмов и границ отделки — колонкой отметок слева. Стена с 5 и более точками или с мелкими звеньями привязок показана двумя видами: архитектурная развёртка (мебель, отделка, проёмы, высоты) и вид «Привязки» на отдельном листе — точки и выводы с марками, одна цепочка по осям и таблица привязок (каждая точка — строка).
3. У знака электроточки: марка (Р — розетка, S — выключатель, Св — светильник, ЭВ — вывод кабеля), ×N — число постов в рамке, гр. — группа щита, Н — высота оси от чистого пола, мм; группы по клавишам выключателя — на листе выключателей.
4. Схема мебели, приборов и декора не является технической документацией для производства мебели; габариты — по паспортам изделий.
5. Двери скрытого монтажа — полотно в плоскости стены, отделка стены по полотну, плинтус прерывается у короба (узел — на листе узлов).

1000 мм · печать 1:1

Изм.	Кол.уч	Лист	№ док.	Подп.	Дата
Разраб.		Кырлан А.С.			04.11.26
Пров.					
ГИП					
Н. контр.					
Утв.					

ГД-2026-012-АИ

Дом 120 м²

Общая площадь 147,36* м² · * размеры приняты, не замерены (реестр — л. 7–9, К-1)

Дизайн-проект интерьера	Стадия	Лист	Листов
	РП	128	175

Развёртка стены В. Холл с лестницей (пом. 2)

М 1:20

Кырлан Александр Сергеевич


выпуск 04.11.2026 № 4dfa962484 · стр. 132 из 180

Развёртка стены Г. Холл с лестницей (пом. 2)

Холл с лестницей (пом. 2) · вид изнутри помещения · размеры в мм, отметки в м от ±0,000 (чистый пол 1-го этажа)


ПРЕДВАРИТЕЛЬНО · не для производства работ · открыто пунктов: 11 (реестр — л. 7–9)

Развёртка стены Г

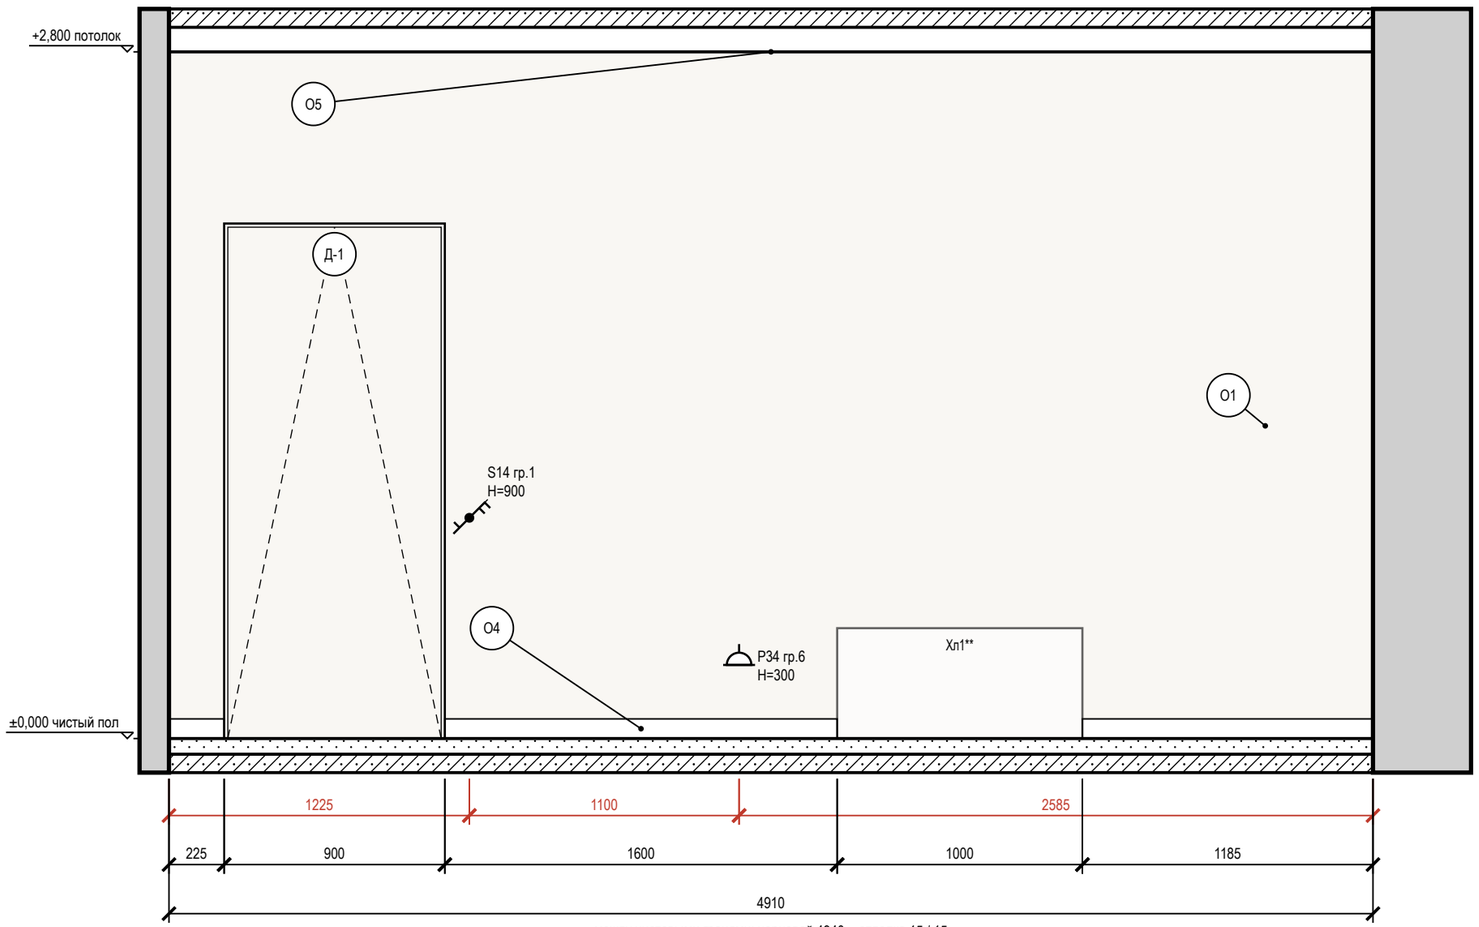

между чистовыми гранями: черновой 4940 − отделка 15 / 15

Схема развёрток (М 1:100)

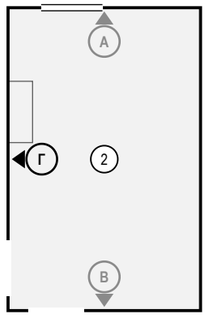

Условные обозначения

- розетка с заземляющим контактом; у знака — марка, ×N постов в рамке, гр. — группа щита, H — высота оси, мм
- выключатель одноклавишный
- выключатель двухклавишный (флажков — по числу клавиш)
- выключатель с проходной или перекрёстной клавишей (обратный флажок); тип клавиши — в подписи
- привязки точек и выводов от угла и от пола, мм
- мебель и приборы — фасад по расстановке (условно)
- дверь скрытого монтажа: полотно в плоскости стены (узел — на листе узлов)
- стены и перекрытия в сечении
- окраска: тон — цвет по коду производителя (условно)
- О1 — марка отделки по реестру отделки альбома
- А — марка развёртки: буква стены, стрелка — взгляд

Ведомость отделки (на листе)

Марка	Поверхность	Материал, изделие	Цвет, код	Кол.
О1	стены	окраска, Tikkurila, матовая, подготовка Q3	Tikkurila G503 «Calla»	11,9 м²
О4	плинтус	плинтус МДФ, h 80 мм, аналог: плинтус МДФ под покраску 80×16	Tikkurila G503 «Calla»	3 м
О5	потолок	окраска, Little Greene Absolute Matt, глубокоматовая, подготовка Q3	Little Greene No. 222 «Loft White»	15,5 м²

Допущения и предложения на листе

Основа листа: взаимное расположение помещений, контур дома 9600 × 8000 и раскладка этажей подобраны проектировщиком под габариты помещений брифа; обмер и проект АР — задание (К-1); высота потолка 2900 мм — по брифу, не замерена; перекрытие 330 мм и отметка 2-го этажа +3,230 приняты; проект КР — задание (К-2); наружные стены 400 мм, перегородки 120 мм приняты (в брифе толщин нет) (К-1); разрешённая мощность 15 кВт принята по типовым ТУ для частного дома (К-4); подрайон климата не задан — принят не северный (жилые от 2,5 м) (К-7).
Знак «*» — принято, не замерено и не подтверждено (замерить на объекте): К-1: окно пом. 2 (стена А) — окно: место, ширина, высота и подоконник приняты по брифу, стена — по раскладке проектировщика (К-1), не замерены.
Знак «**» — предложение проектировщика, заказчиком не утверждено (согласовать с заказчиком): ИЗ-2: Хл1 — Было под окном стены А (700…1700) на радиаторе Рд3 (500…1700): прибор в корпусе.
См. лист открытых вопросов (лист 7, записи К-1, К-2, К-4; лист 8, запись К-7; лист 9, запись ИЗ-2).

Примечания

1. Развёртки — вид на стену изнутри помещения, по часовой стрелке; расположение — на схеме листа и на листе 116; размеры — в мм по чистовым поверхностям; отметки — в м от ±0,000 (чистый пол 1-го этажа); высоты H — от чистого пола помещения до оси изделия, у декора — до центра.
2. Красная цепочка — привязки электроточек и выводов по осям от угла чистовых стен; высота H — у знака, от чистого пола до оси; высоты мебели, проёмов и границ отделки — колонкой отметок слева. Стена с 5 и более точками или с мелкими звеньями привязок показана двумя видами: архитектурная развёртка (мебель, отделка, проёмы, высоты) и вид «Привязки» на отдельном листе — точки и выводы с марками, одна цепочка по осям и таблица привязок (каждая точка — строка).
3. У знака электроточки: марка (Р — розетка, S — выключатель, Св — светильник, ЭВ — вывод кабеля), ×N — число постов в рамке, гр. — группа щита, H — высота оси от чистого пола, мм; группы по клавишам выключателя — на листе выключателей.
4. Схема мебели, приборов и декора не является технической документацией для производства мебели; габариты — по паспортам изделий.
5. Двери скрытого монтажа — полотно в плоскости стены, отделка стены по полотну, плинтус прерывается у короба (узел — на листе узлов).

1000 мм · печать 1:1

Изм.	Кол.уч	Лист	№ док.	Подп.	Дата
Разраб.		Кырлан А.С.			04.11.26
Пров.					
ГИП					
Н. контр.					
Утв.					

ГД-2026-012-АИ

Дом 120 м²

Общая площадь 147,36* м² · * размеры приняты, не замерены (реестр — л. 7–9, К-1)

Дизайн-проект интерьера

Стадия	Лист	Листов
РП	129	175

Развёртка стены Г. Холл с лестницей (пом. 2)

М 1:25

Кырлан Александр Сергеевич


выпуск 04.11.2026 № 4dfa962484 · стр. 133 из 180

Развёртка стены А. Кабинет (пом. 3)

Кабинет (пом. 3) · вид изнутри помещения · размеры в мм, отметки в м от ±0,000 (чистый пол 1-го этажа)


ПРЕДВАРИТЕЛЬНО · не для производства работ · открыто пунктов: 11 (реестр — л. 7–9)

Развёртка стены А

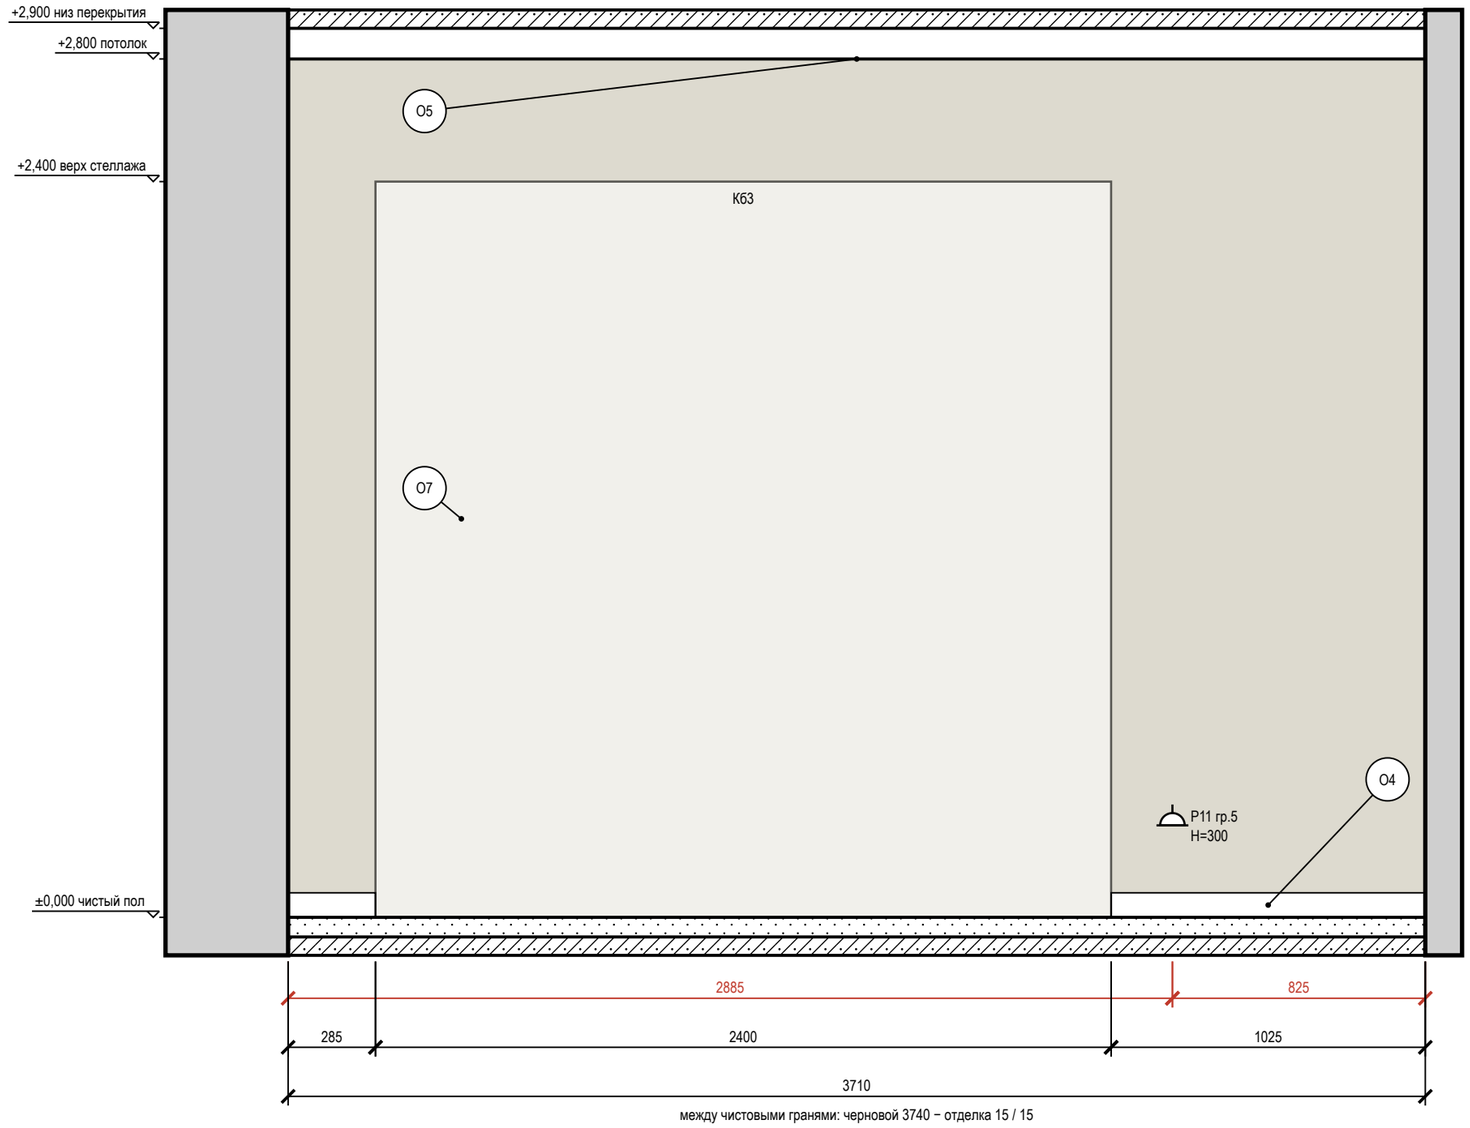

между чистовыми гранями: черновой 3740 − отделка 15 / 15

Схема развёрток (М 1:100)

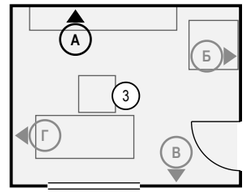

Условные обозначения

- розетка с заземляющим контактом; у знака — марка, ×N постов в рамке, гр. — группа щита, H — высота оси, мм
- привязки точек и выводов от угла и от пола, мм
- мебель и приборы — фасад по расстановке (условно)
- стены и перекрытия в сечении
- окраска: тон — цвет по коду производителя (условно)
- О1 — марка отделки по реестру отделки альбома
- А — марка развёртки: буква стены, стрелка — взгляд

Ведомость отделки (на листе)

Марка	Поверхность	Материал, изделие	Цвет, код	Кол.
О4	плинтус	плинтус МДФ, h 80 мм, аналог: плинтус МДФ под покраску 80×16	Tikkurila G503 «Calla»	1,3 м
О5	потолок	окраска, Little Greene Absolute Matt, глубокоматовая, подготовка Q3	Little Greene No. 222 «Loft White»	11 м²
О7	акцентная стена	окраска, Tikkurila, матовая, подготовка Q3	NCS S 5020-G90Y «Олива»	10,4 м²

Допущения и предложения на листе

Основа листа: взаимное расположение помещений, контур дома 9600 × 8000 и раскладка этажей подобраны проектировщиком под габариты помещений брифа; обмер и проект АР — задание (К-1); высота потолка 2900 мм — по брифу, не замерена; перекрытие 330 мм и отметка 2-го этажа +3,230 приняты; проект КР — задание (К-2); наружные стены 400 мм, перегородки 120 мм приняты (в брифе толщин нет) (К-1); разрешённая мощность 15 кВт принята по типовым ТУ для частного дома (К-4); подрайон климата не задан — принят не северный (жилые от 2,5 м) (К-7).

Знак «*» — принято, не замерено и не подтверждено (замерить на объекте): К-1: окно пом. 3 (стена В) — окно: место, ширина, высота и подоконник приняты по брифу, стена — по раскладке проектировщика (К-1), не замерены; дверь пом. 3 (стена Б) — проём: место и ширина приняты проектировщиком по брифу (раскладка этажей — К-1), не замерены.

См. лист открытых вопросов (лист 7, записи К-1, К-2, К-4; лист 8, запись К-7).

Примечания

1. Развёртки — вид на стену изнутри помещения, по часовой стрелке; расположение — на схеме листа и на листе 116; размеры — в мм по чистовым поверхностям; отметки — в м от ±0,000 (чистый пол 1-го этажа); высоты H — от чистого пола помещения до оси изделия, у декора — до центра.
2. Красная цепочка — привязки электроточек и выводов по осям от угла чистовых стен; высота H — у знака, от чистого пола до оси; высоты мебели, проёмов и границ отделки — колонкой отметок слева. Стена с 5 и более точками или с мелкими звеньями привязок показана двумя видами: архитектурная развёртка (мебель, отделка, проёмы, высоты) и вид «Привязки» на отдельном листе — точки и выводы с марками, одна цепочка по осям и таблица привязок (каждая точка — строка).
3. У знака электроточки: марка (Р — розетка, S — выключатель, Св — светильник, ЭВ — вывод кабеля), ×N — число постов в рамке, гр. — группа щита, H — высота оси от чистого пола, мм; группы по клавишам выключателя — на листе выключателей.
4. Схема мебели, приборов и декора не является технической документацией для производства мебели; габариты — по паспортам изделий.
5. Потолок — у каждой стены свой, по плану потолков (ПТ3); ступени — зоной, кромка короба перед нишей — тонкой линией; в поле потолка: ПТ4 +2,650.

1000 мм · печать 1:1

Изм.	Кол.уч	Лист	№ док.	Подп.	Дата
Разраб.		Кырлан А.С.			04.11.26
Пров.					
ГИП					
Н. контр.					
Утв.					

ГД-2026-012-АИ

Дом 120 м²

Общая площадь 147,36* м² · * размеры приняты, не замерены (реестр — л. 7–9, К-1)

Дизайн-проект интерьера

Стадия	Лист	Листов
РП	130	175

Развёртка стены А. Кабинет (пом. 3)

М 1:20

Кырлан Александр Сергеевич


выпуск 04.11.2026 № 4dfa962484 · стр. 134 из 180

Развёртка стены Б. Кабинет (пом. 3)

Кабинет (пом. 3) · вид изнутри помещения · размеры в мм, отметки в м от ±0,000 (чистый пол 1-го этажа)


ПРЕДВАРИТЕЛЬНО · не для производства работ · открыто пунктов: 11 (реестр — л. 7–9)

Развёртка стены Б

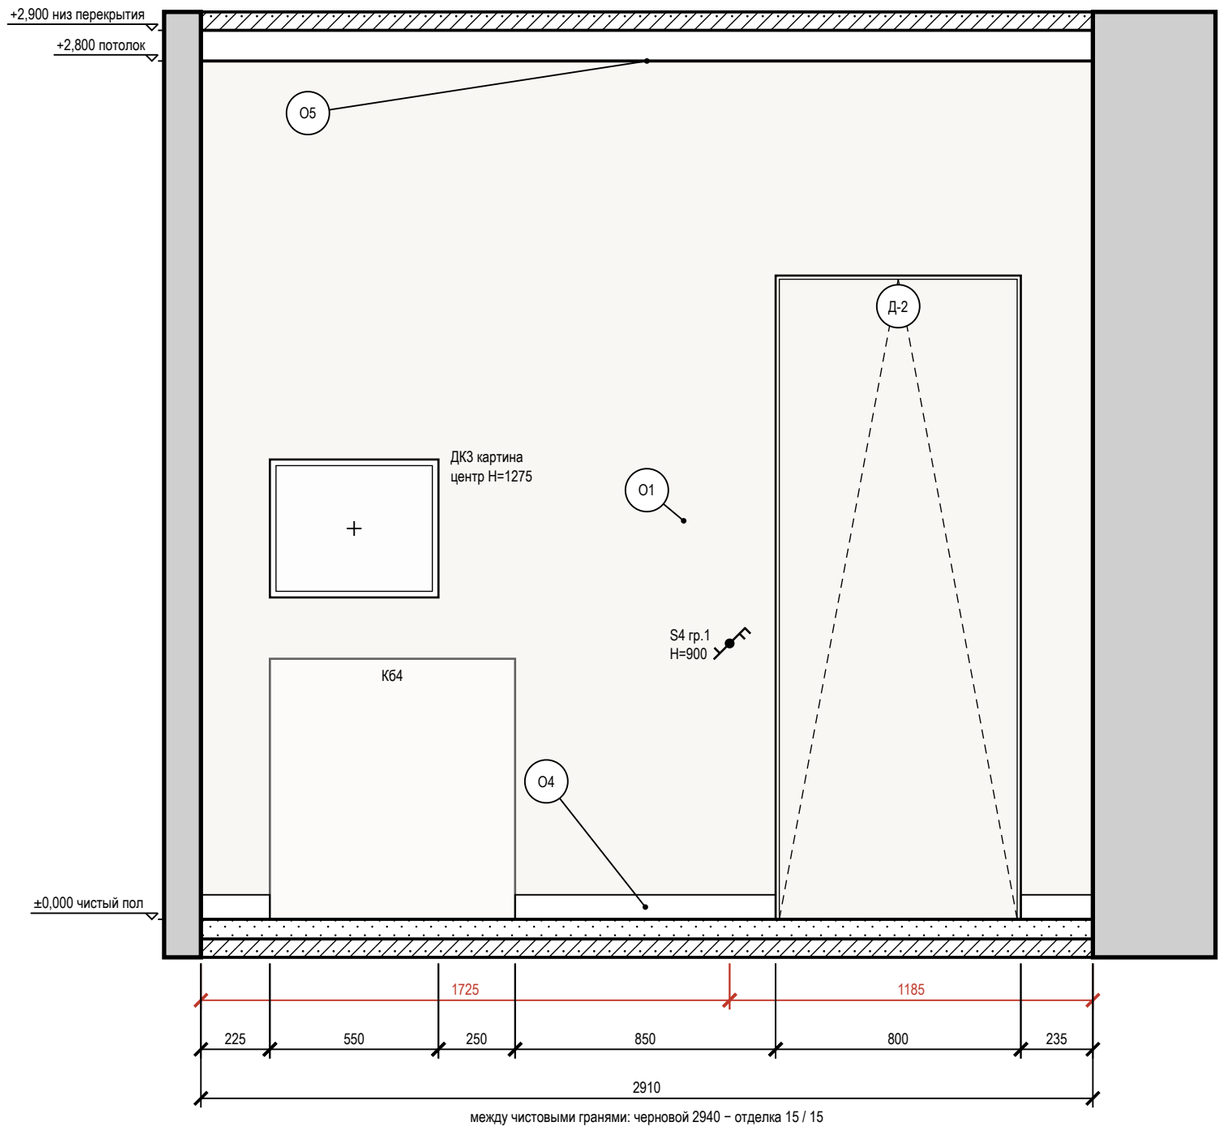

между чистовыми гранями: черновой 2940 − отделка 15 / 15

Схема развёрток (М 1:100)

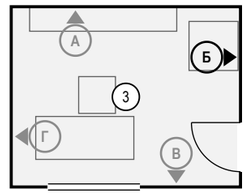

Условные обозначения

- выключатель одноклавишный
- выключатель двухклавишный (флажков — по числу клавиш)
- выключатель с проходной или перекрёстной клавишей (обратный флажок); тип клавиши — в подписи
- привязки точек и выводов от угла и от пола, мм
- мебель и приборы — фасад по расстановке (условно)
- картина (декор): марка Д, крест — центр, Н — высота центра, мм
- дверь скрытого монтажа: полотно в плоскости стены (узел — на листе узлов)
- стены и перекрытия в сечении
- окраска: тон — цвет по коду производителя (условно)
- О1 — марка отделки по реестру отделки альбома
- А — марка развёртки: буква стены, стрелка — взгляд

Ведомость отделки (на листе)

Марка	Поверхность	Материал, изделие	Цвет, код	Кол.
О1	стены	окраска, Tikkurila, матовая, подготовка Q3	Tikkurila G503 «Calla»	6,5 м²
О4	плинтус	плинтус МДФ, h 80 мм, аналог: плинтус МДФ под покраску 80×16	Tikkurila G503 «Calla»	1,3 м
О5	потолок	окраска, Little Greene Absolute Matt, глубокоматовая, подготовка Q3	Little Greene No. 222 «Loft White»	11 м²

Допущения и предложения на листе. Основа листа: взаимное расположение помещений, контур дома 9600 × 8000 и раскладка этажей подобраны проектировщиком под габариты помещений брифа; обмер и проект АР — задание (К-1); высота потолка 2900 мм — по брифу, не замерена; перекрытие 330 мм и отметка 2-го этажа +3,230 приняты; проект КР — задание (К-2); наружные стены 400 мм, перегородки 120 мм приняты (в брифе толщин нет) (К-1); разрешённая мощность 15 кВт принята по типовым ТУ для частного дома (К-4); подрайон климата не задан — принят не северный (жилые от 2,5 м) (К-7). Знак «*» — принято, не замерено (замерить): К-1: окно пом. 3 (стена В), дверь пом. 3 (стена Б). См. лист открытых вопросов (лист 7, записи К-1, К-2, К-4; лист 8, запись К-7).

Примечания

1. Развёртки — вид на стену изнутри помещения, по часовой стрелке; расположение — на схеме листа и на листе 116; размеры — в мм по чистовым поверхностям; отметки — в м от ±0,000 (чистый пол 1-го этажа); высоты Н — от чистого пола помещения до оси изделия, у декора — до центра.
2. Красная цепочка — привязки электроточек и выводов по осям от угла чистовых стен; высота Н — у знака, от чистого пола до оси; высоты мебели, проёмов и границ отделки — колонкой отметок слева. Стена с 5 и более точками или с мелкими звеньями привязок показана двумя видами: архитектурная развёртка (мебель, отделка, проёмы, высоты) и вид «Привязки» на отдельном листе — точки и выводы с марками, одна цепочка по осям и таблица привязок (каждая точка — строка).
3. У знака электроточки: марка (Р — розетка, S — выключатель, Св — светильник, ЭВ — вывод кабеля), ×N — число постов в рамке, гр. — группа щита, Н — высота оси от чистого пола, мм; группы по клавишам выключателя — на листе выключателей.
4. Схема мебели, приборов и декора не является технической документацией для производства мебели; габариты — по паспортам изделий.
5. Картины и зеркала крепить к основанию по паспорту изделия (закладные и анкеры — в перечне скрытых работ); крест — ось центра предмета.
6. Двери скрытого монтажа — полотно в плоскости стены, отделка стены по полотну, плинтус прерывается у короба (узел — на листе узлов).
7. Потолок — у каждой стены свой, по плану потолков (ПТ3); ступени — зоной, кромка короба перед нишей — тонкой линией; в поле потолка: ПТ4 +2,650.

1000 мм · печать 1:1

Изм.	Кол.уч	Лист	№ док.	Подп.	Дата
Разраб.		Кырлан А.С.			04.11.26
Пров.					
ГИП					
Н. контр.					
Утв.					

ГД-2026-012-АИ

Дом 120 м²

Общая площадь 147,36* м² · * размеры приняты, не замерены (реестр — л. 7–9, К-1)

Дизайн-проект интерьера	Стадия	Лист	Листов
	РП	131	175

Развёртка стены Б. Кабинет (пом. 3)

М 1:20

Кырлан Александр Сергеевич


выпуск 04.11.2026 № 4dfa962484 · стр. 135 из 180

Развёртка стены В. Кабинет (пом. 3)

Кабинет (пом. 3) · вид изнутри помещения · размеры в мм, отметки в м от ±0,000 (чистый пол 1-го этажа)


ПРЕДВАРИТЕЛЬНО · не для производства работ · открыто пунктов: 11 (реестр — л. 7–9)

Развёртка стены В

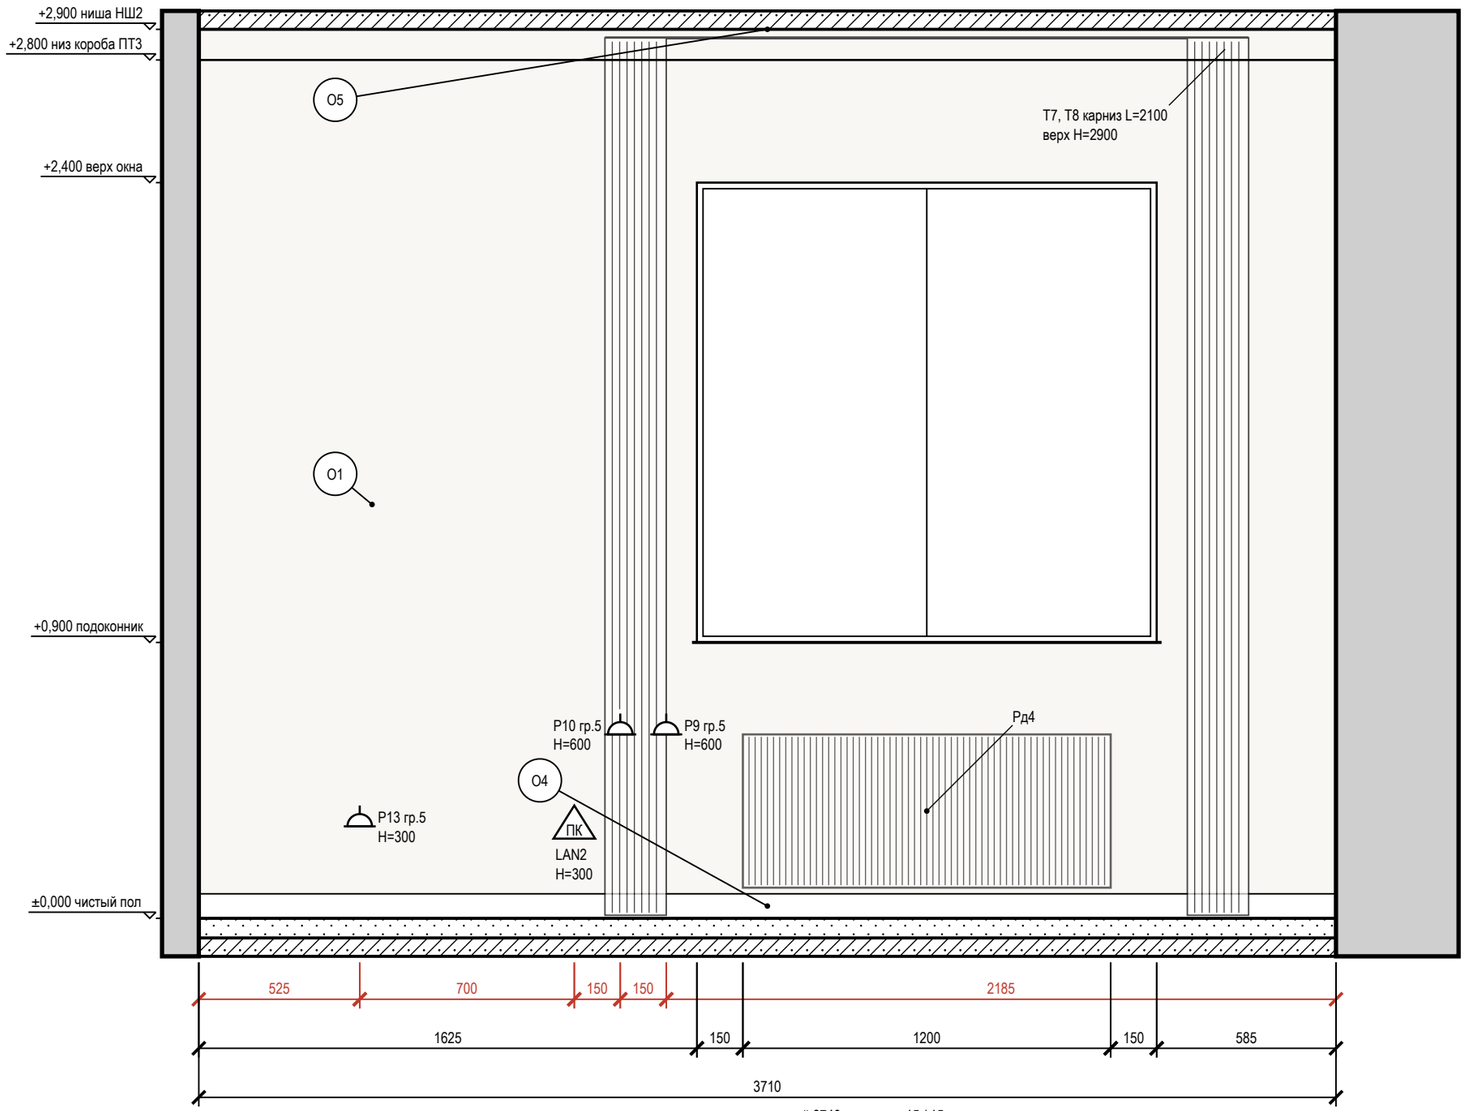

между чистовыми гранями: черновой 3740 − отделка 15 / 15

Схема развёрток (М 1:100)

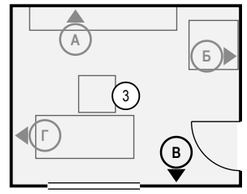

Условные обозначения

- розетка с заземляющим контактом; у знака — марка, ×N постов в рамке, гр. — группа щита, H — высота оси, мм
- ПК — розетка компьютерная RJ45
- привязки точек и выводов от угла и от пола, мм
- мебель и приборы — фасад по расстановке (условно)
- карниз (шина) и шторы в собранном виде: марка T, длина L, верх H
- окно: проём, рама, подоконник
- радиатор отопления; марка — по плану отопления
- стены и перекрытия в сечении
- окраска: тон — цвет по коду производителя (условно)
- О1 — марка отделки по реестру отделки альбома
- А — марка развёртки: буква стены, стрелка — взгляд

Ведомость отделки (на листе)

Марка	Поверхность	Материал, изделие	Цвет, код	Кол.
О1	стены	окраска, Tikkurila, матовая, подготовка Q3	Tikkurila G503 «Calla»	8,5 м²
О4	плинтус	плинтус МДФ, h 80 мм, аналог: плинтус МДФ под покраску 80×16	Tikkurila G503 «Calla»	3,7 м
О5	потолок	окраска, Little Greene Absolute Matt, глубокоматовая, подготовка Q3	Little Greene No. 222 «Loft White»	11 м²

Допущения и предложения на листе. Основа листа: взаимное расположение помещений, контур дома 9600 × 8000 и раскладка этажей подобраны проектировщиком под габариты помещений брифа; обмер и проект АР — задание (К-1); высота потолка 2900 мм — по брифу, не замерена; перекрытие 330 мм и отметка 2-го этажа +3,230 приняты; проект КР — задание (К-2); наружные стены 400 мм, перегородки 120 мм приняты (в брифе толщин нет) (К-1); разрешённая мощность 15 кВт принята по типовым ТУ для частного дома (К-4); подрайон климата не задан — принят не северный (жилые от 2,5 м) (К-7). Знак «*» — принято, не замерено (замерить): К-1: окно пом. 3 (стена В), дверь пом. 3 (стена Б). См. лист открытых вопросов (лист 7, записи К-1, К-2, К-4; лист 8, запись К-7; лист 9, запись ИЗ-2).

Примечания

1. Развёртки — вид на стену изнутри помещения, по часовой стрелке; расположение — на схеме листа и на листе 116; размеры — в мм по чистовым поверхностям; отметки — в м от ±0,000 (чистый пол 1-го этажа); высоты H — от чистого пола помещения до оси изделия, у декора — до центра.
2. Красная цепочка — привязки электроточек и выводов по осям от угла чистовых стен; высота H — у знака, от чистого пола до оси; высоты мебели, проёмов и границ отделки — колонкой отметок слева. Стена с 5 и более точками или с мелкими звеньями привязок показана двумя видами: архитектурная развёртка (мебель, отделка, проёмы, высоты) и вид «Привязки» на отдельном листе — точки и выводы с марками, одна цепочка по осям и таблица привязок (каждая точка — строка).
3. У знака электроточки: марка (Р — розетка, S — выключатель, Св — светильник, ЭВ — вывод кабеля), ×N — число постов в рамке, гр. — группа щита, H — высота оси от чистого пола, мм; группы по клавишам выключателя — на листе выключателей.
4. Схема мебели, приборов и декора не является технической документацией для производства мебели; габариты — по паспортам изделий.
5. Карнизы (шины) — по ведомости текстиля декоратора: длина L и верх H на развёртке — те же числа, что в ведомости; крепление — до окраски потолка.
6. Потолок — у каждой стены свой, по плану потолков (НШ2, ПТ3); ступени — зоной, кромка короба перед нишей — тонкой линией; в поле потолка: ПТ4 +2,650.
7. Линии узора (швы плитки, складки штор, рёбра радиаторов) прерываются у знаков и выносок — просвет между линиями не менее 0,7 мм.

1000 мм · печать 1:1

Изм.	Кол.уч	Лист	№ док.	Подп.	Дата
Разраб.		Кырлан А.С.			04.11.26
Пров.					
ГИП					
Н. контр.					
Утв.					

ГД-2026-012-АИ

Дом 120 м²

Общая площадь 147,36* м² · * размеры приняты, не замерены (реестр — л. 7–9, К-1)

Дизайн-проект интерьера	Стадия	Лист	Листов
	РП	132	175

Развёртка стены В. Кабинет (пом. 3)

М 1:20


Кырлан Александр Сергеевич

выпуск 04.11.2026 № 4dfa962484 · стр. 136 из 180

Развёртка стены Г. Кабинет (пом. 3)


Кабинет (пом. 3) · вид изнутри помещения · размеры в мм, отметки в м от ±0,000 (чистый пол 1-го этажа)

Развёртка стены Г

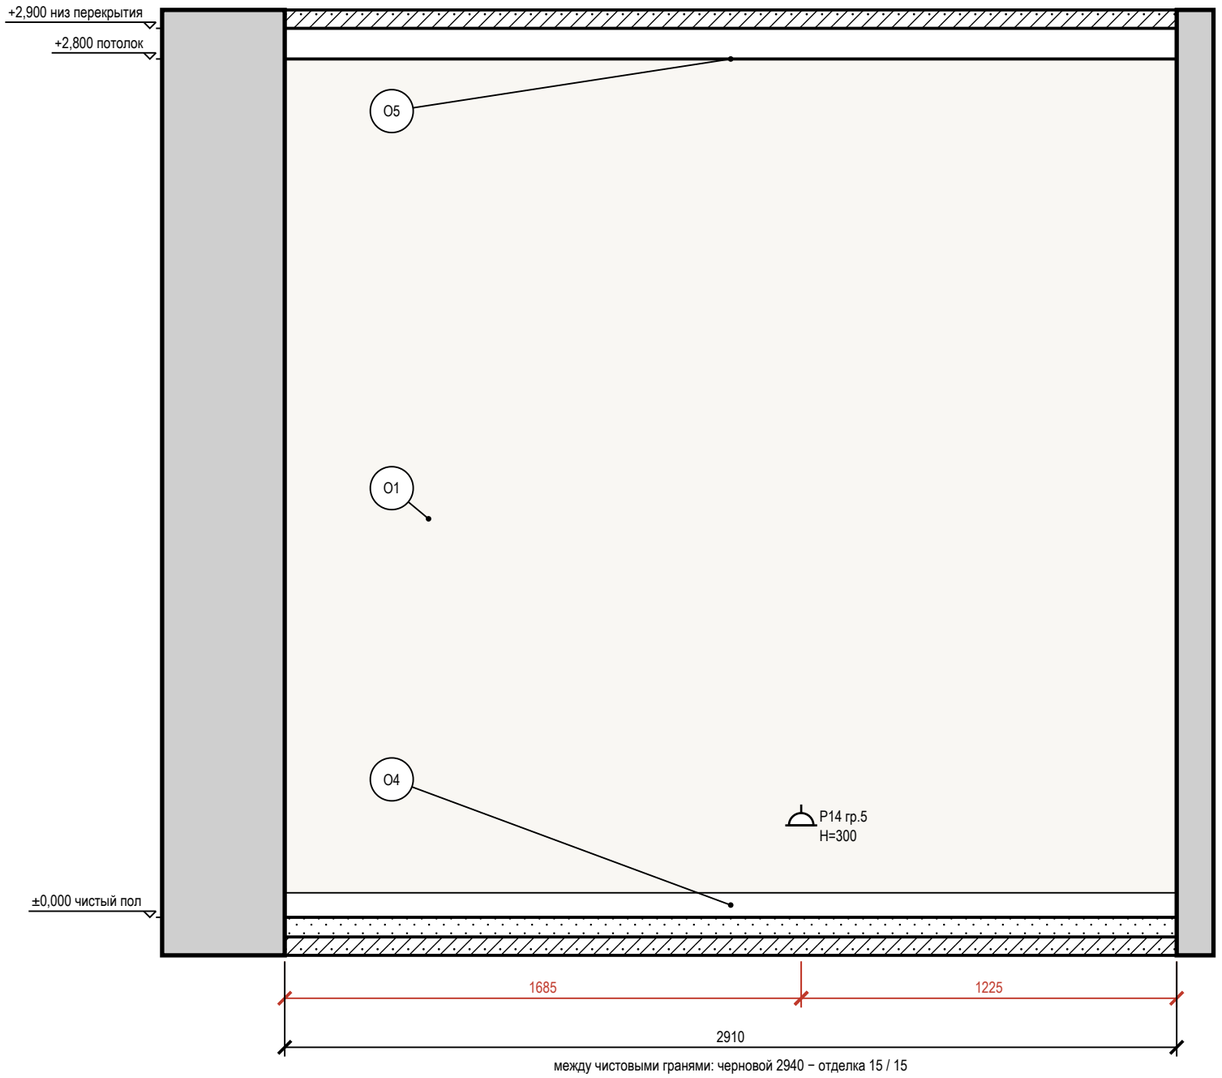

между чистовыми гранями: черновой 2940 − отделка 15 / 15

Схема развёрток (М 1:100)

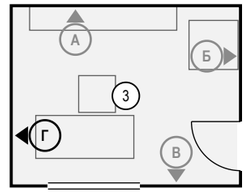

Условные обозначения

- розетка с заземляющим контактом; у знака — марка, ×N постов в рамке, гр. — группа щита, Н — высота оси, мм
- привязки точек и выводов от угла и от пола, мм
- мебель и приборы — фасад по расстановке (условно)
- стены и перекрытия в сечении
- окраска: тон — цвет по коду производителя (условно)
- О1 — марка отделки по реестру отделки альбома
- А — марка развёртки: буква стены, стрелка — взгляд

Ведомость отделки (на листе)

Марка	Поверхность	Материал, изделие	Цвет, код	Кол.
О1	стены	окраска, Tikkurila, матовая, подготовка Q3	Tikkurila G503 «Calla»	8,1 м²
О4	плинтус	плинтус МДФ, h 80 мм, аналог: плинтус МДФ под покраску 80×16	Tikkurila G503 «Calla»	2,9 м
О5	потолок	окраска, Little Greene Absolute Matt, глубокоматовая, подготовка Q3	Little Greene No. 222 «Loft White»	11 м²

Допущения и предложения на листе

Основа листа: взаимное расположение помещений, контур дома 9600 × 8000 и раскладка этажей подобраны проектировщиком под габариты помещений брифа; обмер и проект АР — задание (К-1); высота потолка 2900 мм — по брифу, не замерена; перекрытие 330 мм и отметка 2-го этажа +3,230 приняты; проект КР — задание (К-2); наружные стены 400 мм, перегородки 120 мм приняты (в брифе толщин нет) (К-1); разрешённая мощность 15 кВт принята по типовым ТУ для частного дома (К-4); подрайон климата не задан — принят не северный (жилые от 2,5 м) (К-7).
Знак «*» — принято, не замерено и не подтверждено (замерить на объекте): К-1: окно пом. 3 (стена В) — окно: место, ширина, высота и подоконник приняты по брифу, стена — по раскладке проектировщика (К-1), не замерены; дверь пом. 3 (стена Б) — проём: место и ширина приняты проектировщиком по брифу (раскладка этажей — К-1), не замерены.
См. лист открытых вопросов (лист 7, записи К-1, К-2, К-4; лист 8, запись К-7).

Примечания

1. Развёртки — вид на стену изнутри помещения, по часовой стрелке; расположение — на схеме листа и на листе 116; размеры — в мм по чистовым поверхностям; отметки — в м от ±0,000 (чистый пол 1-го этажа); высоты Н — от чистого пола помещения до оси изделия, у декора — до центра.
2. Красная цепочка — привязки электроточек и выводов по осям от угла чистовых стен; высота Н — у знака, от чистого пола до оси; высоты мебели, проёмов и границ отделки — колонкой отметок слева. Стена с 5 и более точками или с мелкими звеньями привязок показана двумя видами: архитектурная развёртка (мебель, отделка, проёмы, высоты) и вид «Привязки» на отдельном листе — точки и выводы с марками, одна цепочка по осям и таблица привязок (каждая точка — строка).
3. У знака электроточки: марка (Р — розетка, S — выключатель, Св — светильник, ЭВ — вывод кабеля), ×N — число постов в рамке, гр. — группа щита, Н — высота оси от чистого пола, мм; группы по клавишам выключателя — на листе выключателей.
4. Схема мебели, приборов и декора не является технической документацией для производства мебели; габариты — по паспортам изделий.
5. Потолок — у каждой стены свой, по плану потолков (ПТ3); ступени — зоной, кромка короба перед нишей — тонкой линией; в поле потолка: ПТ4 +2,650.

1000 мм · печать 1:1

Изм.	Кол.уч	Лист	№ док.	Подп.	Дата
Разраб.		Кырлан А.С.			04.11.26
Пров.					
ГИП					
Н. контр.					
Утв.					

ГД-2026-012-АИ

Дом 120 м²

Общая площадь 147,36* м² · * размеры приняты, не замерены (реестр — л. 7–9, К-1)

Дизайн-проект интерьера	Стадия	Лист	Листов
	РП	133	175

Развёртка стены Г. Кабинет (пом. 3)

М 1:20

Кырлан Александр Сергеевич


выпуск 04.11.2026 № 4dfa962484 · стр. 137 из 180

Развёртки стен А, Б. Санузел гостевой (пом. 4)

Санузел гостевой (пом. 4) · вид изнутри помещения · размеры в мм, отметки в м от ±0,000 (чистый пол 1-го этажа)


ПРЕДВАРИТЕЛЬНО · не для производства работ · открыто пунктов: 11 (реестр — л. 7–9)

Развёртка стены А

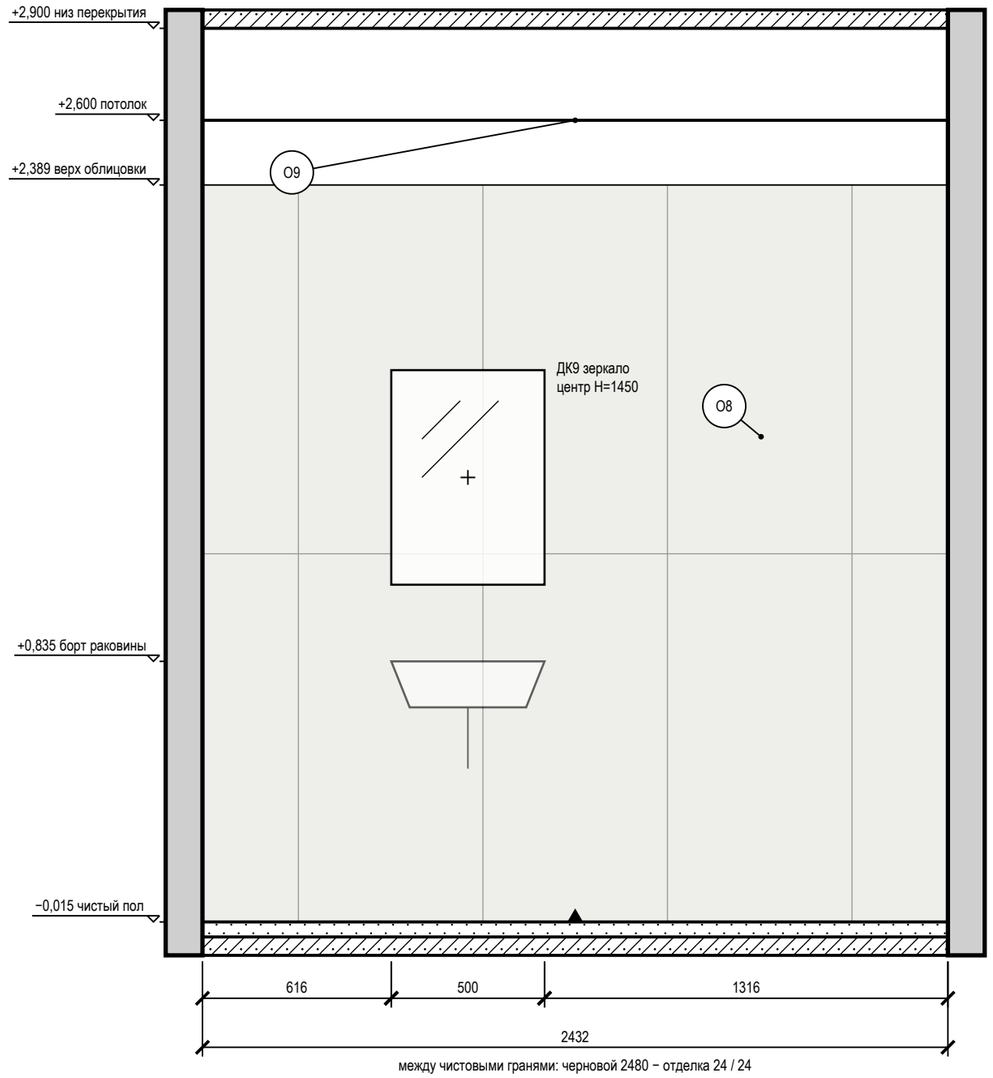


между чистовыми гранями: черновой 2480 − отделка 24 / 24

Развёртка стены Б

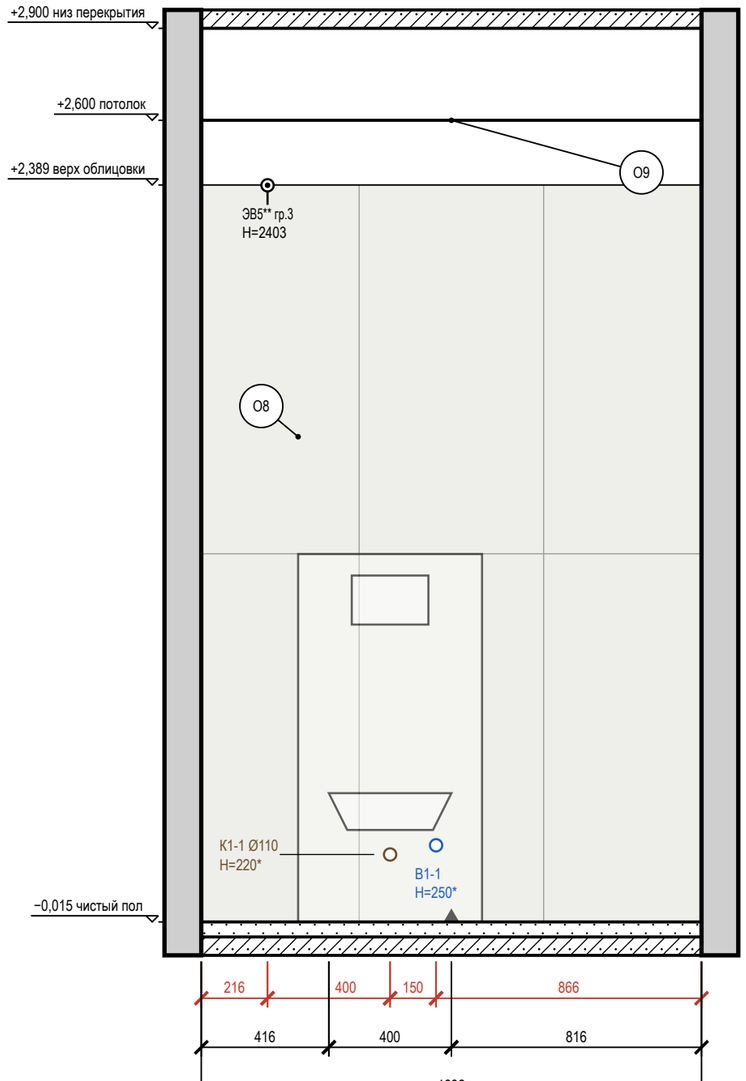

между чистовыми гранями: черновой 1680 − отделка 24 / 24

Схема развёрток (М 1:100)

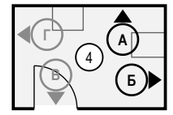

Условные обозначения

- вывод кабеля для подключения прибора (без розетки), марка ЭВ
- вывод В1 (код — в ведомости привязок)
- вывод К1 (код — в ведомости привязок)
- привязки точек и выводов от угла и от пола, мм
- мебель и приборы — фасад по расстановке (условно)
- зеркало: марка Д, крест — центр, Н — высота центра, мм
- стены и перекрытия в сечении
- плитка: сетка швов по формату, ▲ — ось старта
- О1 — марка отделки по реестру отделки альбома
- А — марка развёртки: буква стены, стрелка — взгляд

Допущения и предложения на листе

Основа листа: взаимное расположение помещений, контур дома 9600 × 8000 и раскладка этажей подобраны проектировщиком под габариты помещений брифа; обмер и проект АР — задание (К-1); высота потолка 2900 мм — по брифу, не замерена; перекрытие 330 мм и отметка 2-го этажа +3,230 приняты; проект КР — задание (К-2); наружные стены 400 мм, перегородки 120 мм приняты (в брифе толщин нет) (К-1); разрешённая мощность 15 кВт принята по типовым ТУ для частного дома (К-4); подрайон климата не задан — принят не северный (жилые от 2,5 м) (К-7).

Знак «*» — принято, не замерено и не подтверждено (замерить на объекте): К-1: дверь пом. 4 (стена В) — проём: место и ширина приняты проектировщиком по брифу (раскладка этажей — К-1), не замерены.

Знак «**» — предложение проектировщика, заказчиком не утверждено (согласовать с заказчиком): ЭВ5 — по образцу: Добавлены выводы к вентиляторам: ЭВ4 (ВР1, ванная) и ЭВ5 (ВР3, санузел 2) — группа 3, высота 2389 мм, включение с основным светом, таймер выбега в вентиляторе; и коробки уравнивания потенциалов КУП1 (ванная) и КУП2 (санузел 2) — высота 300 мм, у входа, вне зон 0–2, проводник от шины РЕ щита ЩК …; сдвиг под раскладку плитки стены Б на 14 мм выше — ось на шве или в центре плитки, привязка по таблице листа.

См. лист открытых вопросов (лист 7, записи К-1, К-2, К-4; лист 8, запись К-7).

Примечания

1. Развёртки — вид на стену изнутри помещения, по часовой стрелке; расположение — на схеме листа и на листе 116; размеры — в мм по чистовым поверхностям; отметки — в м от ±0,000 (чистый пол 1-го этажа); высоты Н — от чистого пола помещения до оси изделия, у декора — до центра.
2. Красная цепочка — привязки электроточек и выводов по осям от угла чистовых стен; высота Н — у знака, от чистого пола до оси; высоты мебели, проёмов и границ отделки — колонкой отметок слева. Стена с 5 и более точками или с мелкими звеньями привязок показана двумя видами: архитектурная развёртка (мебель, отделка, проёмы, высоты) и вид «Привязки» на отдельном листе — точки и выводы с марками, одна цепочка по осям и таблица привязок (каждая точка — строка).
3. Стена А показана двумя видами: здесь — архитектурная развёртка (мебель, отделка, проёмы, высоты), электроточки и выводы ВК с привязками и таблицей — на листе 135 («Привязки»).
4. У знака электроточки: марка (Р — розетка, S — выключатель, Св — светильник, ЭВ — вывод кабеля), ×N — число постов в рамке, гр. — группа щита, Н — высота оси от чистого пола, мм; группы по клавишам выключателя — на листе выключателей.
5. Схема мебели, приборов и декора не является технической документацией для производства мебели; габариты — по паспортам изделий (* — высота не задана в проекте, показана по типовому изделию).
6. Выводы ВК — коды и высоты по листу выводов сантехники; * — высота принята по типовой практике монтажа, окончательно — по паспорту прибора.
7. Облицовка — по сетке швов 2 мм, раскладка от оси стены (треугольник у пола), целые ряды от пола; подрезки — по листу раскладки плитки.
8. Гидроизоляция в 2 слоя, заход на стены 200 мм — до облицовки, с актом скрытых работ и тестом проливом (узел — на листе узлов).
9. Картины и зеркала крепить к основанию по паспорту изделия (закладные и анкеры — в перечне скрытых работ); крест — ось центра предмета.

1000 мм · печать 1:1

Изм.	Кол.уч	Лист	№ док.	Подп.	Дата
Разраб.		Кырлан А.С.			04.11.26
Пров.					
ГИП					
Н. контр.					
Утв.					

ГД-2026-012-АИ

Дом 120 м²

Общая площадь 147,36* м² · * размеры приняты, не замерены (реестр — л. 7–9, К-1)

Дизайн-проект интерьера	Стадия	Лист	Листов
	РП	134	175

Развёртки стен А, Б. Санузел гостевой (пом. 4)

М 1:20

Кырлан Александр Сергеевич

выпуск 04.11.2026 № 4dfa962484 · стр. 138 из 180

Привязки электроточек и выводов ВК, стена А. Санузел гостевой (пом. 4)

Санузел гостевой (пом. 4) · вид изнутри помещения · привязки в мм, отметки в м · к развёртке на листе 134

ПРЕДВАРИТЕЛЬНО · не для производства работ · открыто пунктов: 11 (реестр — л. 7–9)

Развёртка стены А: электроточки и выводы

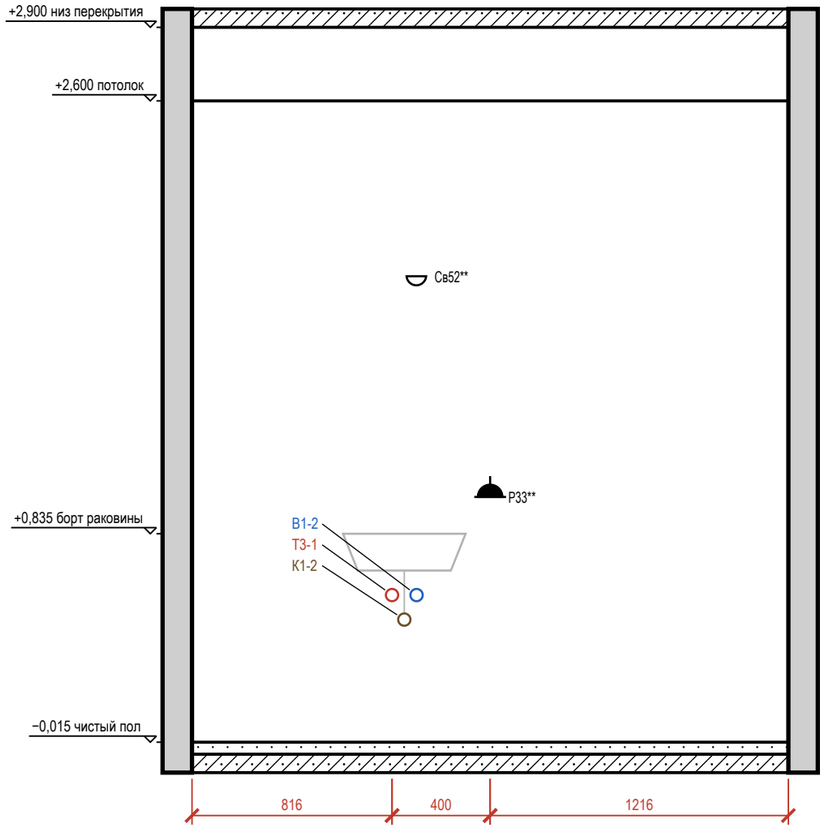


Таблица привязок электроточек и выводов

Марка	Назначение	От угла, мм	Н от пола, мм	Примечание
Т3-1	горячая вода — умывальник	816	600*	межос. 100
К1-2	канализация — умывальник	866	500*	Ø50
Св52**	светильник настенный	915	1900	гр. 3
В1-2	холодная вода — умывальник	916	600*	межос. 100
Р33**	розетка: фен у умывальника	1216	1000	гр. 16, IP44

Условные обозначения

- розетка влагозащищённая IP44
- светильник настенный (бра), Н — высота оси
- вывод В1 (код — в ведомости привязок)
- вывод Т3 (код — в ведомости привязок)
- вывод К1 (код — в ведомости привязок)
- привязки точек и выводов от угла и от пола, мм
- марка развёртки: буква стены, стрелка — взгляд

Схема развёрток (М 1:50)

Примечания

1. Вид «Привязки» стены А — электроточки и выводы ВК; архитектурная развёртка (мебель, отделка, проёмы, высоты) — на листе 134, расположение — на листе 116. Мебель и приборы — подложкой для ориентира; их марки и обозначения мебели, проёмов и стен — там же.
2. Привязки — в мм: по горизонтали от левого чистового угла стены до оси изделия, Н — от чистого пола до оси; все точки — в таблице привязок. Красная цепочка — привязки по осям; точки ближе 150 мм одна к другой в цепочку не дробятся — их привязки только в таблице.
3. У знака — марка электроточки (Р — розетка, S — выключатель, Св — светильник, ЭВ — вывод кабеля); посты в рамке и группа щита — в графе «Примечание»; группы по клавишам выключателя — на листе выключателей.
4. Коды выводов ВК: В1 — холодная вода, Т3 — горячая вода, К1 — канализация; номер после дефиса — номер вывода на листе выводов сантехники; * — высота принята по типовой практике монтажа, окончательно — по паспорту прибора.

Допущения и предложения на листе

Основа листа: взаимное расположение помещений, контур дома 9600 × 8000 и раскладка этажей подобраны проектировщиком под габариты помещений брифа; обмер и проект АР — задание (К-1); высота потолка 2900 мм — по брифу, не замерена; перекрытие 330 мм и отметка 2-го этажа +3,230 приняты; проект КР — задание (К-2); наружные стены 400 мм, перегородки 120 мм приняты (в брифе толщин нет) (К-1); разрешённая мощность 15 кВт принята по типовым ТУ для частного дома (К-4); подрайон климата не задан — принят не северный (жилые от 2,5 м) (К-7).

Знак «*» — принято, не замерено и не подтверждено (замерить на объекте): К-1: дверь пом. 4 (стена В) — проём: место и ширина приняты проектировщиком по брифу (раскладка этажей — К-1), не замерены.

Знак «**» — предложение проектировщика, заказчиком не утверждено (согласовать с заказчиком): Св52 — Сдвиг под раскладку плитки стены А на 49 мм вдоль стены — ось на шве или в центре плитки, привязка по таблице листа; ИЗ-2: Р33 — по образцу: Розетка Р33 на высоте 1100 мм, вне шва плитки.

См. лист открытых вопросов (лист 7, записи К-1, К-2, К-4; лист 8, запись К-7; лист 9, запись ИЗ-2).

1000 мм · печать 1:1

Изм.	Кол.уч	Лист	№ док.	Подп.	Дата
Разраб.		Кырлан А.С.			04.11.26
Пров.					
ГИП					
Н. контр.					
Утв.					

ГД-2026-012-АИ

Дом 120 м²

Общая площадь 147,36* м² · * размеры приняты, не замерены (реестр — л. 7–9, К-1)

Дизайн-проект интерьера

Стадия	Лист	Листов
РП	135	175

Привязки электроточек и выводов ВК, стена А. Санузел гостевой (пом. 4)

М 1:25

Кырлан Александр Сергеевич


выпуск 04.11.2026 № 4dfa962484 · стр. 139 из 180

Развёртки стен В, Г. Санузел гостевой (пом. 4)

Санузел гостевой (пом. 4) · вид изнутри помещения · размеры в мм, отметки в м от ±0,000 (чистый пол 1-го этажа)


ПРЕДВАРИТЕЛЬНО · не для производства работ · открыто пунктов: 11 (реестр — л. 7–9)

Развёртка стены В

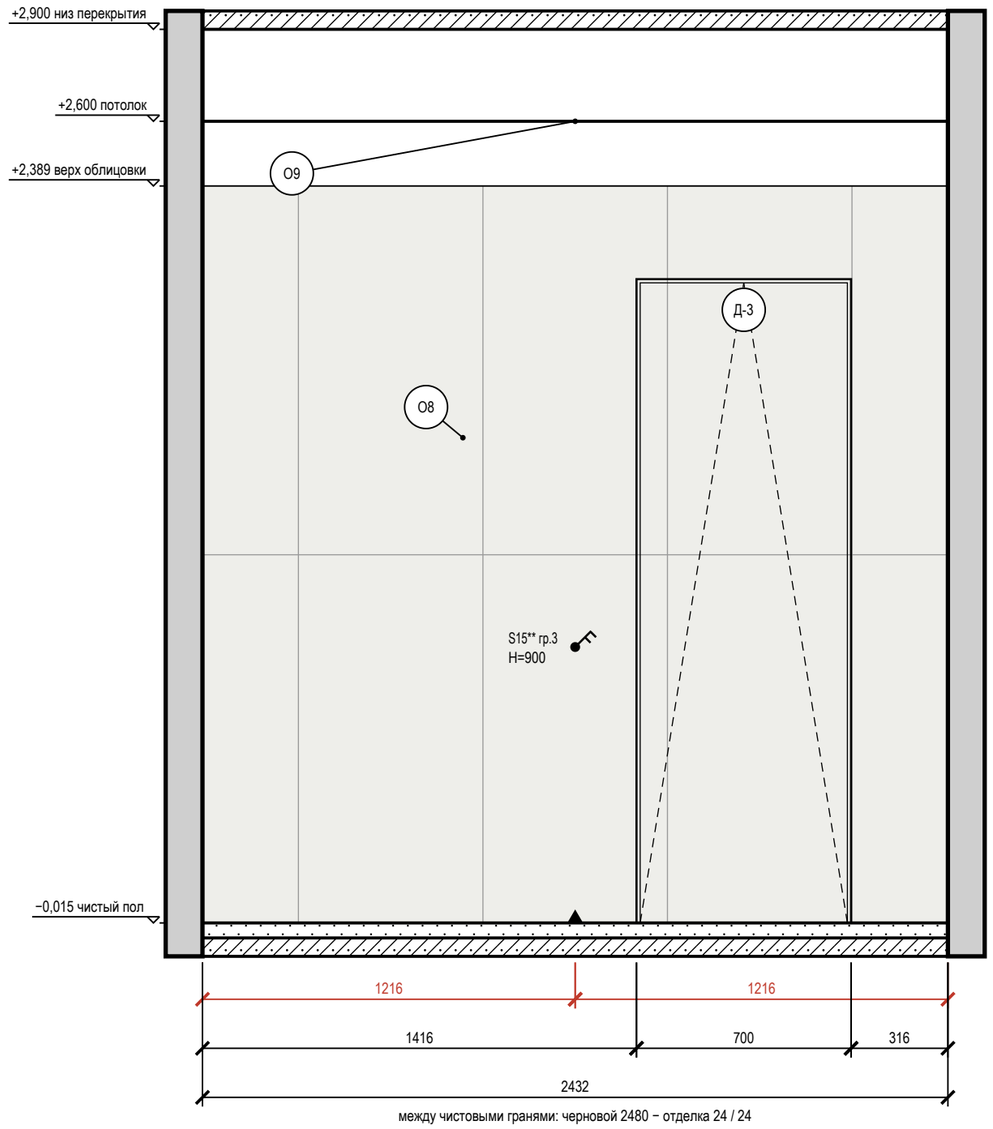


между чистовыми гранями: черновой 2480 − отделка 24 / 24

Развёртка стены Г

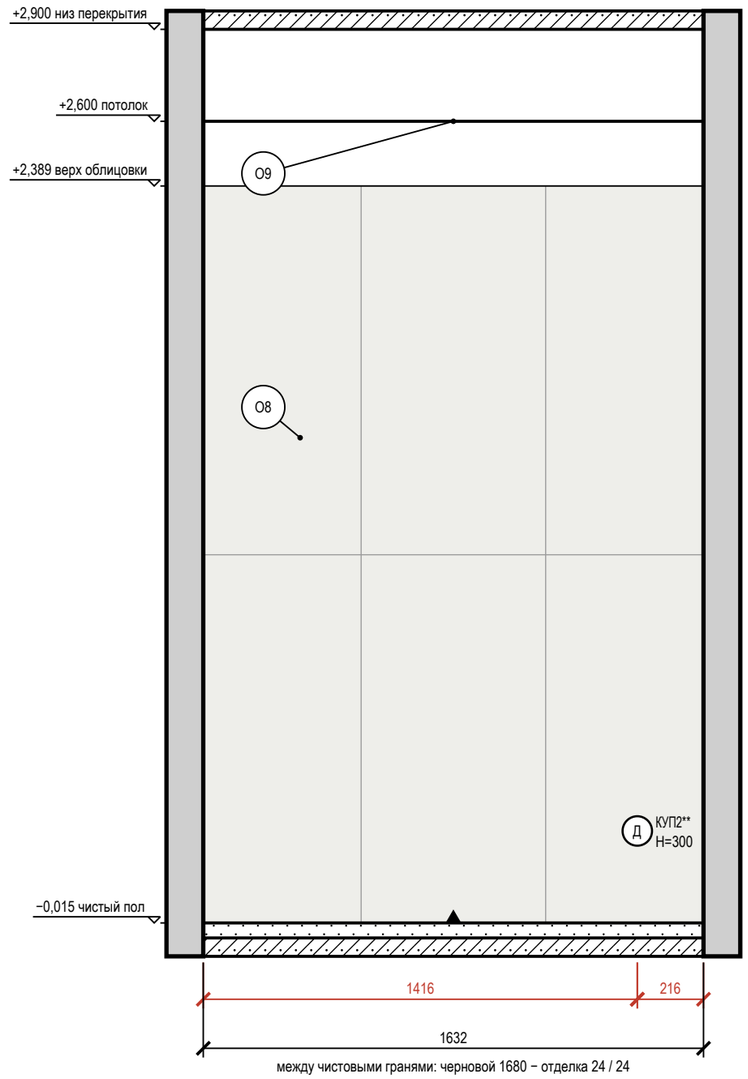

между чистовыми гранями: черновой 1680 − отделка 24 / 24

Схема развёрток (М 1:100)

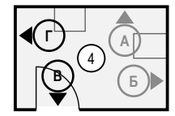

Условные обозначения

- выключатель одноклавишный
- выключатель двухклавишный (флажков — по числу клавиш)
- привязки точек и выводов от угла и от пола, мм
- мебель и приборы — фасад по расстановке (условно)
- дверь скрытого монтажа: полотно в плоскости стены (узел — на листе узлов)
- стены и перекрытия в сечении
- плитка: сетка швов по формату, ▲ — ось старта
- О1 — марка отделки по реестру отделки альбома
- А — марка развёртки: буква стены, стрелка — взгляд

Допущения и предложения на листе

Основа листа: взаимное расположение помещений, контур дома 9600 × 8000 и раскладка этажей подобраны проектировщиком под габариты помещений брифа; обмер и проект АР — задание (К-1); высота потолка 2900 мм — по брифу, не замерена; перекрытие 330 мм и отметка 2-го этажа +3,230 приняты; проект КР — задание (К-2); наружные стены 400 мм, перегородки 120 мм приняты (в брифе толщин нет) (К-1); разрешённая мощность 15 кВт принята по типовым ТУ для частного дома (К-4); подрайон климата не задан — принят не северный (жилые от 2,5 м) (К-7).

Знак «*» — принято, не замерено и не подтверждено (замерить на объекте): К-1: дверь пом. 4 (стена В) — проём: место и ширина приняты проектировщиком по брифу (раскладка этажей — К-1), не замерены.

Знак «**» — предложение проектировщика, заказчиком не утверждено (согласовать с заказчиком): КУП2 — по образцу: Добавлены выводы к вентиляторам: ЭВ4 (ВР1, ванная) и ЭВ5 (ВР3, санузел 2) — группа 3, высота 2389 мм, включение с основным светом, таймер выбега в вентиляторе; и коробки уравнивания потенциалов КУП1 (ванная) и КУП2 (санузел 2) — высота 300 мм, у входа, вне зон 0–2, проводник от шины PE щита ЩК …; S15 — Сдвиг под раскладку плитки стены В на 50 мм вдоль стены — ось на шве или в центре плитки, привязка по таблице листа.

См. лист открытых вопросов (лист 7, записи К-1, К-2, К-4; лист 8, запись К-7).

Примечания

1. Развёртки — вид на стену изнутри помещения, по часовой стрелке; расположение — на схеме листа и на листе 116; размеры — в мм по чистовым поверхностям; отметки — в м от ±0,000 (чистый пол 1-го этажа); высоты Н — от чистого пола помещения до оси изделия, у декора — до центра.
2. Красная цепочка — привязки электроточек и выводов по осям от угла чистовых стен; высота Н — у знака, от чистого пола до оси; высоты мебели, проёмов и границ отделки — колонкой отметок слева. Стена с 5 и более точками или с мелкими звеньями привязок показана двумя видами: архитектурная развёртка (мебель, отделка, проёмы, высоты) и вид «Привязки» на отдельном листе — точки и выводы с марками, одна цепочка по осям и таблица привязок (каждая точка — строка).
3. У знака электроточки: марка (Р — розетка, S — выключатель, Св — светильник, ЭВ — вывод кабеля), ×N — число постов в рамке, гр. — группа щита, Н — высота оси от чистого пола, мм; группы по клавишам выключателя — на листе выключателей.
4. Схема мебели, приборов и декора не является технической документацией для производства мебели; габариты — по паспортам изделий.
5. Облицовка — по сетке швов 2 мм, раскладка от оси стены (треугольник у пола), целые ряды от пола; подрезки — по листу раскладки плитки.
6. Гидроизоляция в 2 слоя, заход на стены 200 мм — до облицовки, с актом скрытых работ и тестом проливом (узел — на листе узлов).
7. Двери скрытого монтажа — полотно в плоскости стены, отделка стены по полотну, плинтус прерывается у короба (узел — на листе узлов).

1000 мм · печать 1:1

						ГД-2026-012-АИ	
						Дом 120 м²	
						Общая площадь 147,36* м² · * размеры приняты, не замерены (реестр — л. 7–9, К-1)	
Изм.	Кол.уч	Лист	№ док.	Подп.	Дата	Дизайн-проект интерьера	Стадия: РП; Лист: 136; Листов: 175
Разраб.		Кырлан А.С.			04.11.26		
Пров.							
ГИП							
						Развёртки стен В, Г. Санузел гостевой (пом. 4) М 1:20	Кырлан Александр Сергеевич
Н. контр.							
Утв.							


выпуск 04.11.2026 № 4dfa962484 · стр. 140 из 180

Развёртка стены А1. Прихожая (пом. 5)

Прихожая (пом. 5) · вид изнутри помещения · размеры в мм, отметки в м от ±0,000 (чистый пол 1-го этажа)

ПРЕДВАРИТЕЛЬНО · не для производства работ · открыто пунктов: 11 (реестр — л. 7–9)

Развёртка стены А1

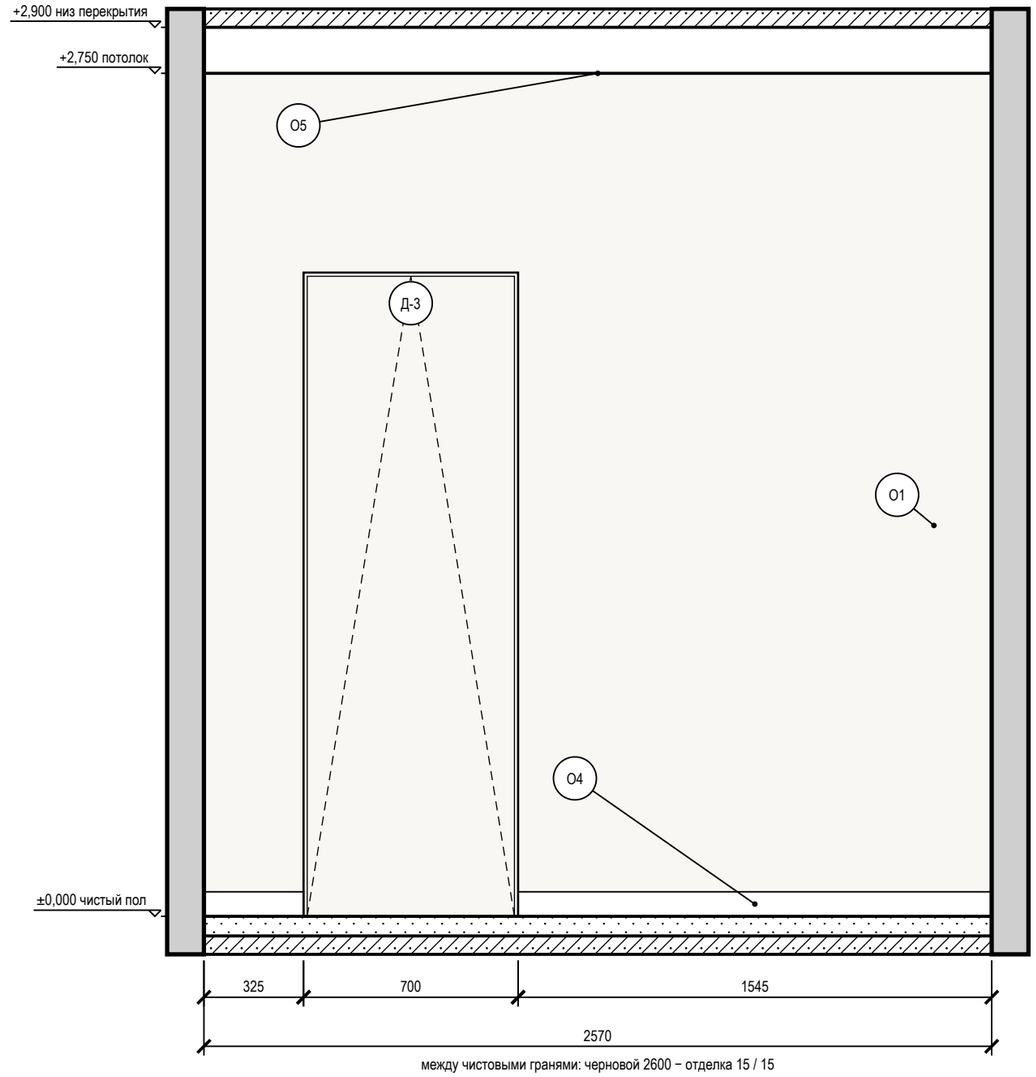

Допущения и предложения на листе


Основа листа: взаимное расположение помещений, контур дома 9600 × 8000 и раскладка этажей подобраны проектировщиком под габариты помещений брифа; обмер и проект АР — задание (К-1); высота потолка 2900 мм — по брифу, не замерена; перекрытие 330 мм и отметка 2-го этажа +3,230 приняты; проект КР — задание (К-2); наружные стены 400 мм, перегородки 120 мм приняты (в брифе толщин нет) (К-1); разрешённая мощность 15 кВт принята по типовым ТУ для частного дома (К-4); подрайон климата не задан — принят не северный (жилые от 2,5 м) (К-7).
Знак «*» — принято, не замерено и не подтверждено (замерить на объекте): К-1: дверь пом. 5 (стена В) — входная дверь: место и ширина проёма приняты проектировщиком по брифу (без плана дома), не замерены; дверь пом. 5 (стена А) — проём: место и ширина приняты проектировщиком по брифу (раскладка этажей — К-1), не замерены.
См. лист открытых вопросов (лист 7, записи К-1, К-2, К-4; лист 8, запись К-7).

Примечания

1. Развёртки — вид на стену изнутри помещения, по часовой стрелке; расположение — на схеме листа и на листе 116; размеры — в мм по чистовым поверхностям; отметки — в м от ±0,000 (чистый пол 1-го этажа); высоты Н — от чистого пола помещения до оси изделия, у декора — до центра.
2. Схема мебели, приборов и декора не является технической документацией для производства мебели; габариты — по паспортам изделий.
3. Двери скрытого монтажа — полотно в плоскости стены, отделка стены по полотну, плинтус прерывается у короба (узел — на листе узлов).

1000 мм · печать 1:1

Схема развёрток (М 1:100)

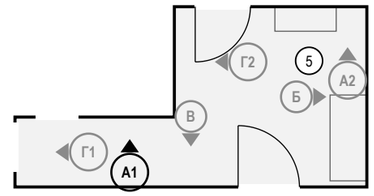

Условные обозначения

- мебель и приборы — фасад по расстановке (условно)
- дверь скрытого монтажа: полотно в плоскости стены (узел — на листе узлов)
- стены и перекрытия в сечении
- окраска: тон — цвет по коду производителя (условно)
- О1 — марка отделки по реестру отделки альбома
- А — марка развёртки: буква стены, стрелка — взгляд

Ведомость отделки (на листе)

Марка	Поверхность	Материал, изделие	Цвет, код	Кол.
О1	стены	окраска, Tikkurila, матовая, подготовка Q3	Tikkurila G503 «Calla»	5,6 м²
О4	плинтус	плинтус МДФ, h 80 мм, аналог: плинтус МДФ под покраску 80×16	Tikkurila G503 «Calla»	1,9 м
О5	потолок	окраска, Little Greene Absolute Matt, глубокоматовая, подготовка Q3	Little Greene No. 222 «Loft White»	12,2 м²

Изм.	Кол.уч	Лист	№ док.	Подп.	Дата
Разраб.		Кырлан А.С.			04.11.26
Пров.					
ГИП					
Н. контр.					
Утв.					

ГД-2026-012-АИ

Дом 120 м²

Общая площадь 147,36* м² · * размеры приняты, не замерены (реестр — л. 7–9, К-1)

Дизайн-проект интерьера

Стадия	Лист	Листов
РП	137	175

Развёртка стены А1. Прихожая (пом. 5)

М 1:20

Кырлан Александр Сергеевич


выпуск 04.11.2026 № 4dfa962484 · стр. 141 из 180

Развёртка стены А2. Прихожая (пом. 5)

Прихожая (пом. 5) · вид изнутри помещения · размеры в мм, отметки в м от ±0,000 (чистый пол 1-го этажа)


ПРЕДВАРИТЕЛЬНО · не для производства работ · открыто пунктов: 11 (реестр — л. 7–9)

Развёртка стены А2

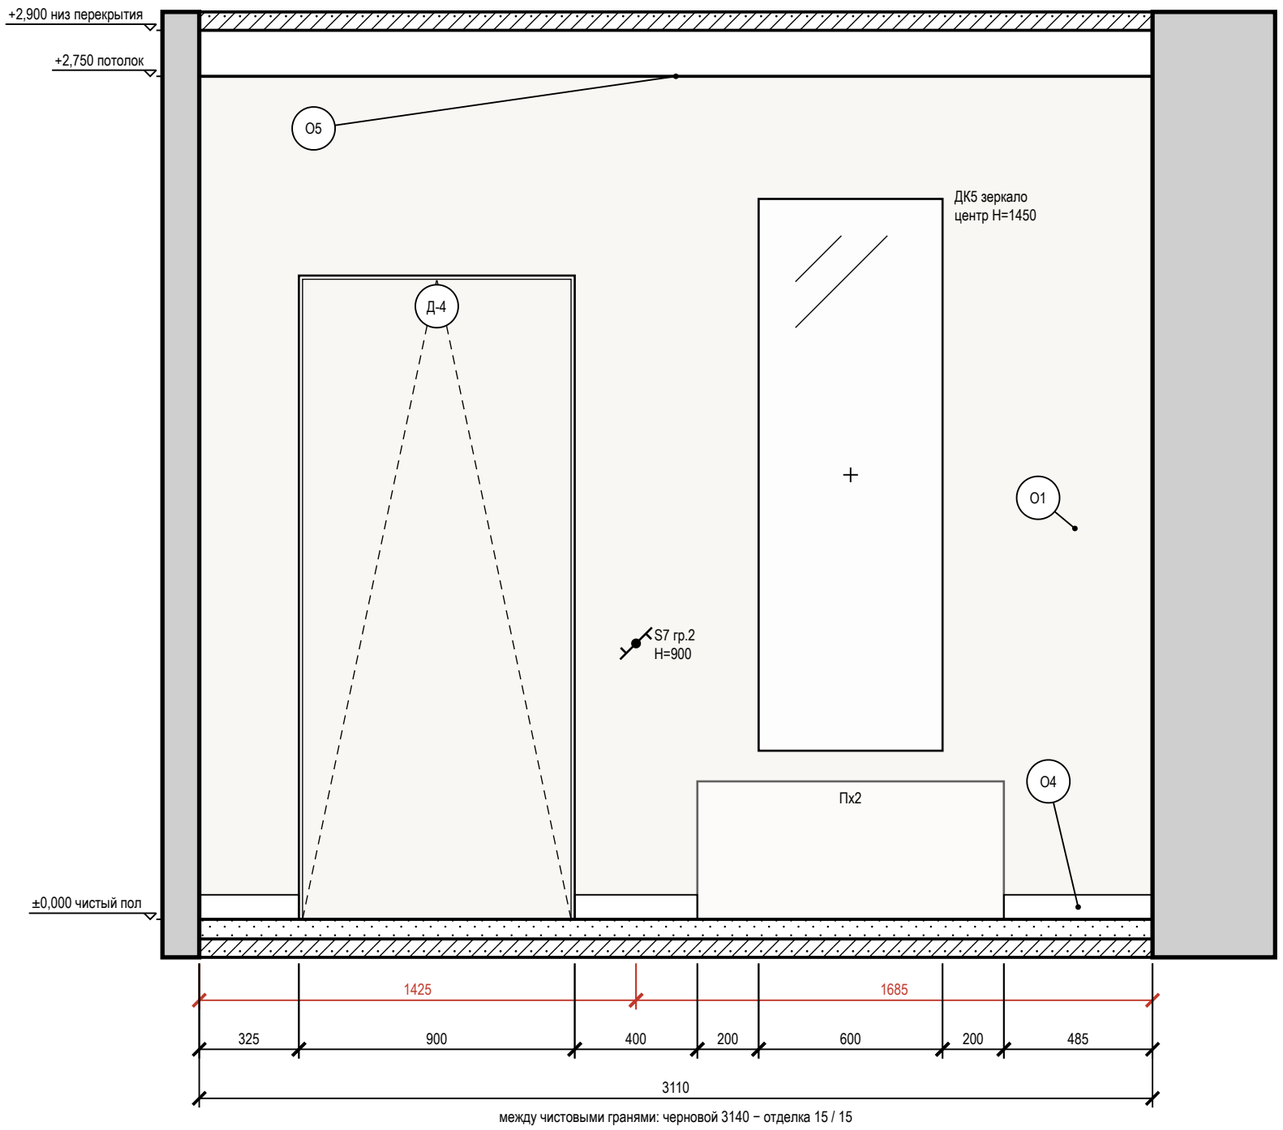

между чистовыми гранями: черновой 3140 − отделка 15 / 15

Схема развёрток (М 1:100)

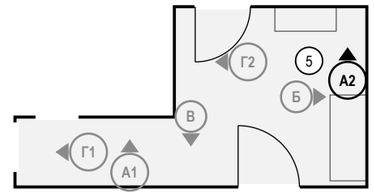

Условные обозначения

- выключатель одноклавишный
- выключатель с проходной или перекрёстной клавишей (обратный флажок); тип клавиши — в подписи
- привязки точек и выводов от угла и от пола, мм
- мебель и приборы — фасад по расстановке (условно)
- зеркало: марка Д, крест — центр, Н — высота центра, мм
- дверь скрытого монтажа: полотно в плоскости стены (узел — на листе узлов)
- стены и перекрытия в сечении
- окраска: тон — цвет по коду производителя (условно)
- О1 — марка отделки по реестру отделки альбома
- А — марка развёртки: буква стены, стрелка — взгляд

Ведомость отделки (на листе)

Марка	Поверхность	Материал, изделие	Цвет, код	Кол.
О1	стены	окраска, Tikkurila, матовая, подготовка Q3	Tikkurila G503 «Calla»	6,7 м²
О4	плинтус	плинтус МДФ, h 80 мм, аналог: плинтус МДФ под покраску 80×16	Tikkurila G503 «Calla»	1,2 м
О5	потолок	окраска, Little Greene Absolute Matt, глубокоматовая, подготовка Q3	Little Greene No. 222 «Loft White»	12,2 м²

Допущения и предложения на листе. Основа листа: взаимное расположение помещений, контур дома 9600 × 8000 и раскладка этажей подобраны проектировщиком под габариты помещений брифа; обмер и проект АР — задание (К-1); высота потолка 2900 мм — по брифу, не замерена; перекрытие 330 мм и отметка 2-го этажа +3,230 приняты; проект КР — задание (К-2); наружные стены 400 мм, перегородки 120 мм приняты (в брифе толщин нет) (К-1); разрешённая мощность 15 кВт принята по типовым ТУ для частного дома (К-4); подрайон климата не задан — принят не северный (жилые от 2,5 м) (К-7). Знак «*» — принято, не замерено (замерить): К-1: дверь пом. 5 (стена В), 5 (А). См. лист открытых вопросов (лист 7, записи К-1, К-2, К-4; лист 8, запись К-7).

Примечания

1. Развёртки — вид на стену изнутри помещения, по часовой стрелке; расположение — на схеме листа и на листе 116; размеры — в мм по чистовым поверхностям; отметки — в м от ±0,000 (чистый пол 1-го этажа); высоты Н — от чистого пола помещения до оси изделия, у декора — до центра.
2. Красная цепочка — привязки электроточек и выводов по осям от угла чистовых стен; высота Н — у знака, от чистого пола до оси; высоты мебели, проёмов и границ отделки — колонкой отметок слева. Стена с 5 и более точками или с мелкими звеньями привязок показана двумя видами: архитектурная развёртка (мебель, отделка, проёмы, высоты) и вид «Привязки» на отдельном листе — точки и выводы с марками, одна цепочка по осям и таблица привязок (каждая точка — строка).
3. У знака электроточки: марка (Р — розетка, S — выключатель, Св — светильник, ЭВ — вывод кабеля), ×N — число постов в рамке, гр. — группа щита, Н — высота оси от чистого пола, мм; группы по клавишам выключателя — на листе выключателей.
4. Схема мебели, приборов и декора не является технической документацией для производства мебели; габариты — по паспортам изделий.
5. Картины и зеркала крепить к основанию по паспорту изделия (закладные и анкеры — в перечне скрытых работ); крест — ось центра предмета.
6. Двери скрытого монтажа — полотно в плоскости стены, отделка стены по полотну, плинтус прерывается у короба (узел — на листе узлов).

1000 мм · печать 1:1

Изм.	Кол.уч	Лист	№ док.	Подп.	Дата
Разраб.		Кырлан А.С.			04.11.26
Пров.					
ГИП					
Н. контр.					
Утв.					

ГД-2026-012-АИ

Дом 120 м²

Общая площадь 147,36* м² · * размеры приняты, не замерены (реестр — л. 7–9, К-1)

Дизайн-проект интерьера

Стадия	Лист	Листов
РП	138	175

Развёртка стены А2. Прихожая (пом. 5)

М 1:20

Кырлан Александр Сергеевич


выпуск 04.11.2026 № 4dfa962484 · стр. 142 из 180

Развёртка стены Б. Прихожая (пом. 5)

Прихожая (пом. 5) · вид изнутри помещения · размеры в мм, отметки в м от ±0,000 (чистый пол 1-го этажа)


ПРЕДВАРИТЕЛЬНО · не для производства работ · открыто пунктов: 11 (реестр — л. 7–9)

Развёртка стены Б

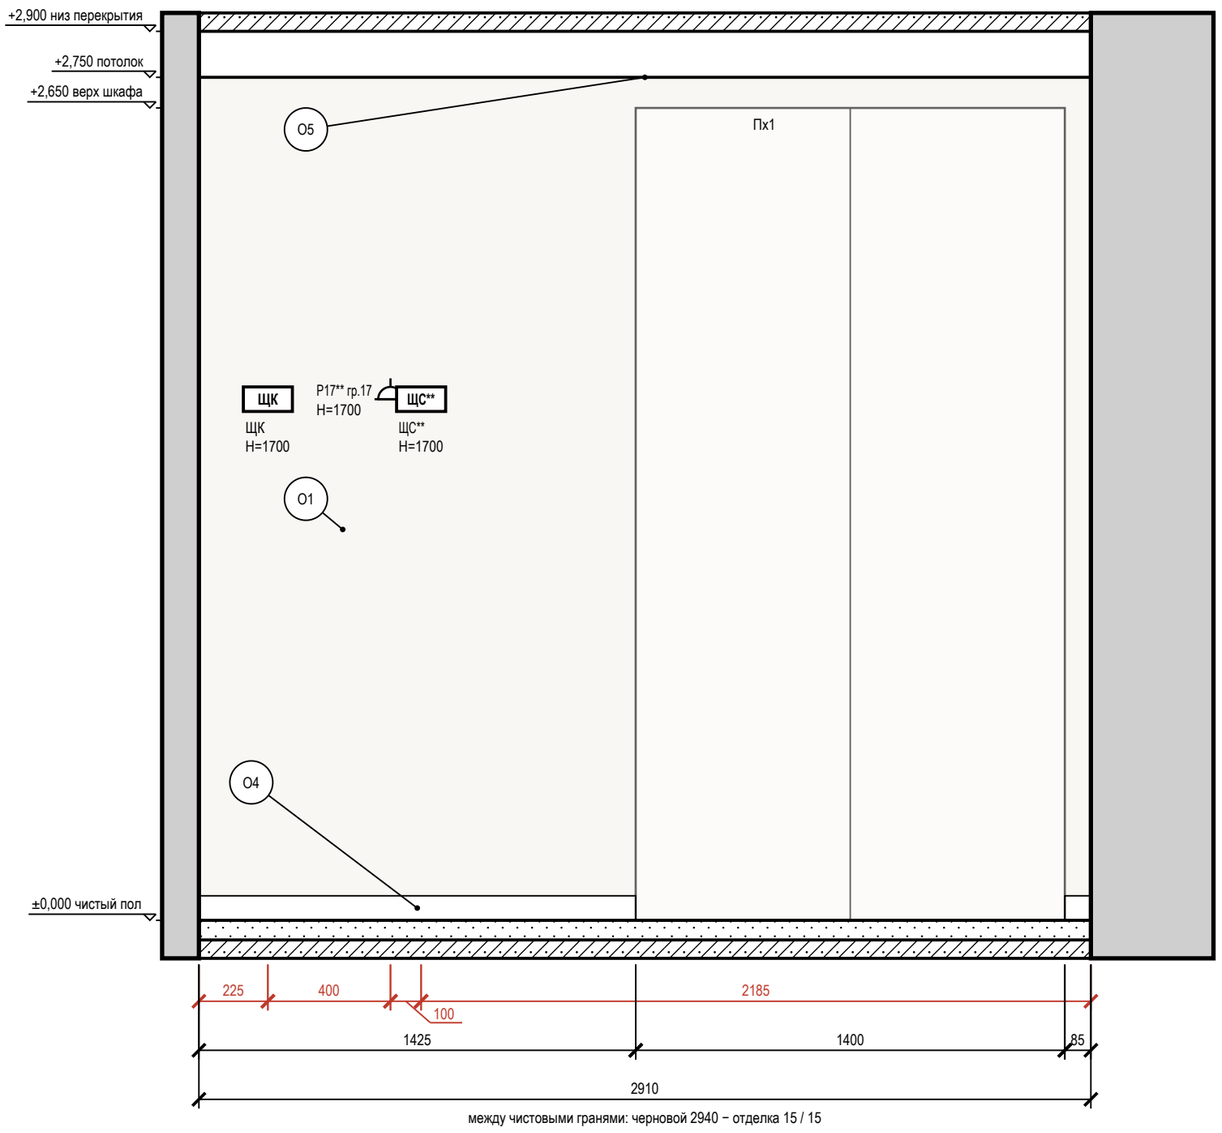

между чистовыми гранями: черновой 2940 − отделка 15 / 15

Схема развёрток (М 1:100)

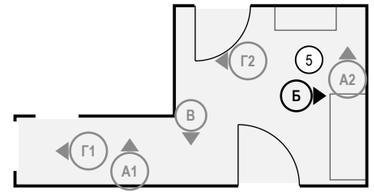

Условные обозначения

- розетка с заземляющим контактом; у знака — марка, ×N постов в рамке, гр. — группа щита, Н — высота оси, мм
- ЩК — щит квартирный
- привязки точек и выводов от угла и от пола, мм
- мебель и приборы — фасад по расстановке (условно)
- стены и перекрытия в сечении
- окраска: тон — цвет по коду производителя (условно)
- О1 — марка отделки по реестру отделки альбома
- А — марка развёртки: буква стены, стрелка — взгляд

Ведомость отделки (на листе)

Марка	Поверхность	Материал, изделие	Цвет, код	Кол.
О1	стены	окраска, Tikkurila, матовая, подготовка Q3	Tikkurila G503 «Calla»	8 м²
О4	плинтус	плинтус МДФ, h 80 мм, аналог: плинтус МДФ под покраску 80×16	Tikkurila G503 «Calla»	1,5 м
О5	потолок	окраска, Little Greene Absolute Matt, глубокоматовая, подготовка Q3	Little Greene No. 222 «Loft White»	12,2 м²

Допущения и предложения на листе. Основа листа: взаимное расположение помещений, контур дома 9600 × 8000 и раскладка этажей подобраны проектировщиком под габариты помещений брифа; обмер и проект АР — задание (К-1); высота потолка 2900 мм — по брифу, не замерена; перекрытие 330 мм и отметка 2-го этажа +3,230 приняты; проект КР — задание (К-2); наружные стены 400 мм, перегородки 120 мм приняты (в брифе толщин нет) (К-1); разрешённая мощность 15 кВт принята по типовым ТУ для частного дома (К-4); подрайон климата не задан — принят не северный (жилые от 2,5 м) (К-7). Знак «*» — принято, не замерено (замерить): К-1: дверь пом. 5 (стена В), 5 (А). Знак «**» — предложено, не утверждено (согласовать): ИЗ-2: Р17, ЩС. См. лист открытых вопросов (лист 7, записи К-1, К-2, К-4; лист 8, запись К-7; лист 9, запись ИЗ-2).

Примечания

1. Развёртки — вид на стену изнутри помещения, по часовой стрелке; расположение — на схеме листа и на листе 116; размеры — в мм по чистовым поверхностям; отметки — в м от ±0,000 (чистый пол 1-го этажа); высоты Н — от чистого пола помещения до оси изделия, у декора — до центра.
2. Красная цепочка — привязки электроточек и выводов по осям от угла чистовых стен; высота Н — у знака, от чистого пола до оси; высоты мебели, проёмов и границ отделки — колонкой отметок слева. Стена с 5 и более точками или с мелкими звеньями привязок показана двумя видами: архитектурная развёртка (мебель, отделка, проёмы, высоты) и вид «Привязки» на отдельном листе — точки и выводы с марками, одна цепочка по осям и таблица привязок (каждая точка — строка).
3. У знака электроточки: марка (Р — розетка, S — выключатель, Св — светильник, ЭВ — вывод кабеля), ×N — число постов в рамке, гр. — группа щита, Н — высота оси от чистого пола, мм; группы по клавишам выключателя — на листе выключателей.
4. Схема мебели, приборов и декора не является технической документацией для производства мебели; габариты — по паспортам изделий.

1000 мм · печать 1:1

Изм.	Кол.уч	Лист	№ док.	Подп.	Дата
Разраб.		Кырлан А.С.			04.11.26
Пров.					
ГИП					
Н. контр.					
Утв.					

ГД-2026-012-АИ

Дом 120 м²

Общая площадь 147,36* м² · * размеры приняты, не замерены (реестр — л. 7–9, К-1)

Дизайн-проект интерьера

Стадия	Лист	Листов
РП	139	175

Развёртка стены Б. Прихожая (пом. 5)

М 1:20

Кырлан Александр Сергеевич


выпуск 04.11.2026 № 4dfa962484 · стр. 143 из 180

Развёртка стены В. Прихожая (пом. 5)

Прихожая (пом. 5) · вид изнутри помещения · размеры в мм, отметки в м от ±0,000 (чистый пол 1-го этажа)

ПРЕДВАРИТЕЛЬНО · не для производства работ · открыто пунктов: 11 (реестр — л. 7–9)

Развёртка стены В

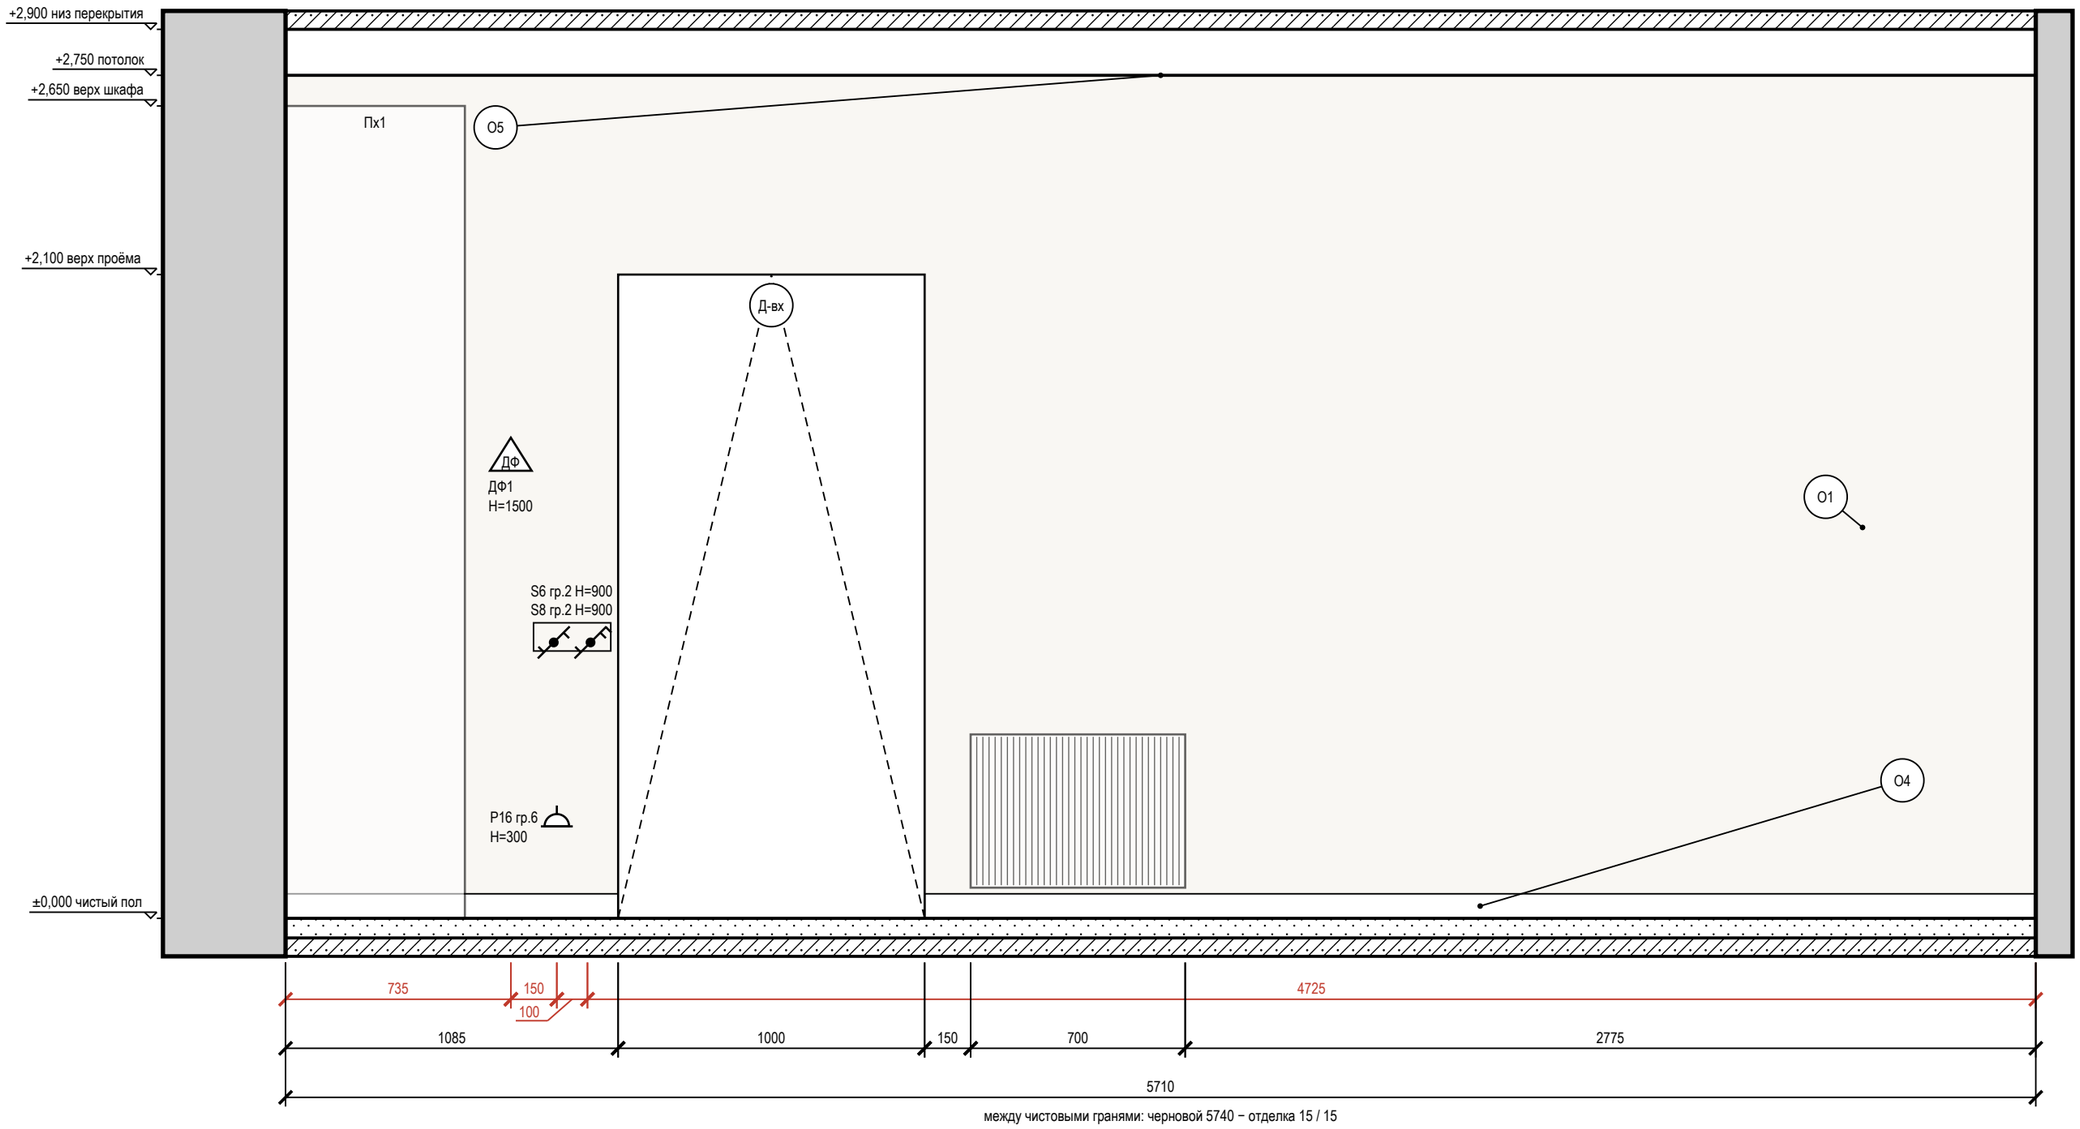

между чистовыми гранями: черновой 5740 − отделка 15 / 15

Условные обозначения

обозначения этого вида, схема развёрток помещения и ведомость отделки — на листе 141

Примечания

1. Развёртки — вид на стену изнутри помещения, по часовой стрелке; расположение — на схеме листа 141 и на листе 116; размеры — в мм по чистовым поверхностям; отметки — в м от ±0,000 (чистый пол 1-го этажа); высоты H — от чистого пола помещения до оси изделия, у декора — до центра.
2. Красная цепочка — привязки электроточек и выводов по осям от угла чистовых стен; высота H — у знака, от чистого пола до оси; высоты мебели, проёмов и границ отделки — колонкой отметок слева. Стена с 5 и более точками или с мелкими звеньями привязок показана двумя видами: архитектурная развёртка (мебель, отделка, проёмы, высоты) и вид «Привязки» на отдельном листе — точки и выводы с марками, одна цепочка по осям и таблица привязок (каждая точка — строка).
3. У знака электроточки: марка (Р — розетка, S — выключатель, Св — светильник, ЭВ — вывод кабеля), ×N — число постов в рамке, гр. — группа щита, H — высота оси от чистого пола, мм; группы по клавишам выключателя — на листе выключателей.
4. Схема мебели, приборов и декора не является технической документацией для производства мебели; габариты — по паспортам изделий.

Допущения и предложения на листе. Знак «*» принято (замерить): дверь пом. 5 (стена В), 5 (А). См. лист открытых вопросов (листы 7–9).

1000 мм · печать 1:1

Изм.	Кол.уч	Лист	№ док.	Подп.	Дата
Разраб.		Кырлан А.С.			04.11.26
Пров.					
ГИП					
Н. контр.					
Утв.					

ГД-2026-012-АИ

Дом 120 м²

Общая площадь 147,36* м² · * размеры приняты, не замерены (реестр — л. 7–9, К-1)

Дизайн-проект интерьера

Стадия	Лист	Листов
РП	140	175

Развёртка стены В. Прихожая (пом. 5)


М 1:20

Кырлан Александр Сергеевич

Развёртка стены В: схема и ведомость отделки. Прихожая (пом. 5)

Прихожая (пом. 5) · к развёртке на листе 140

Схема развёрток (М 1:50)

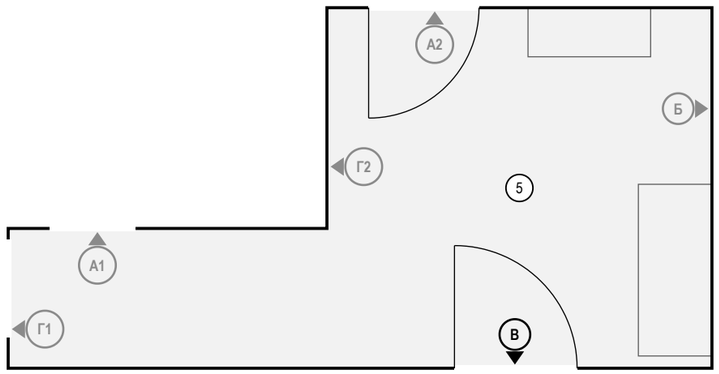

Условные обозначения

- розетка с заземляющим контактом; у знака — марка, ×N постов в рамке, гр. — группа щита, Н — высота оси, мм
- выключатель одноклавишный
- выключатель двухклавишный (флажков — по числу клавиш)
- выключатель с проходной или перекрёстной клавишей (обратный флажок); тип клавиши — в подписи
- ДФ — трубка или монитор домофона
- привязки точек и выводов от угла и от пола, мм
- мебель и приборы — фасад по расстановке (условно)
- дверной проём; марка двери — в кружке
- радиатор отопления; марка — по плану отопления
- стены и перекрытия в сечении
- окраска: тон — цвет по коду производителя (условно)
- О1 — марка отделки по реестру отделки альбома
- А — марка развёртки: буква стены, стрелка — взгляд

Ведомость отделки (на листе)

Марка	Поверхность	Материал, изделие	Цвет, код	Кол.
О1	стены	окраска, Tikkurila, матовая, подготовка Q3	Tikkurila G503 «Calla»	13,6 м²
О4	плинтус	плинтус МДФ, h 80 мм, аналог: плинтус МДФ под покраску 80×16	Tikkurila G503 «Calla»	4,7 м
О5	потолок	окраска, Little Greene Absolute Matt, глубокоматовая, подготовка Q3	Little Greene No. 222 «Loft White»	12,2 м²

Примечания

1. Схема, условные обозначения и ведомость отделки — к развёртке стены В на листе 140: вид в своём масштабе занимает лист целиком.
2. Расположение развёрток всех помещений — на листе 116; полная ведомость отделки — на листах отделочника.

Допущения и предложения на листе

Основа листа: взаимное расположение помещений, контур дома 9600 × 8000 и раскладка этажей подобраны проектировщиком под габариты помещений брифа; обмер и проект АР — задание (К-1); высота потолка 2900 мм — по брифу, не замерена; перекрытие 330 мм и отметка 2-го этажа +3,230 приняты; проект КР — задание (К-2); наружные стены 400 мм, перегородки 120 мм приняты (в брифе толщин нет) (К-1); разрешённая мощность 15 кВт принята по типовым ТУ для частного дома (К-4); подрайон климата не задан — принят не северный (жилые от 2,5 м) (К-7).
Знак «**» — предложение проектировщика, заказчиком не утверждено (согласовать с заказчиком): плинтус пом. 5 — артикул изделия не выбран: позиция описана характеристиками («аналог по характеристикам»), артикул выбирается при закупке.
См. лист открытых вопросов (лист 7, записи К-1, К-2, К-4; лист 8, запись К-7).

Изм.	Кол.уч	Лист	№ док.	Подп.	Дата
Разраб.		Кырлан А.С.			04.11.26
Пров.					
ГИП					
Н. контр.					
Утв.					

ГД-2026-012-АИ

Дом 120 м²

Общая площадь 147,36* м² · * размеры приняты, не замерены (реестр — л. 7–9, К-1)

Дизайн-проект интерьера	Стадия	Лист	Листов
	РП	141	175

Развёртка стены В: схема и ведомость отделки. Прихожая (пом. 5)
М б/м

Кырлан Александр Сергеевич


выпуск 04.11.2026 № 4dfa962484 · стр. 145 из 180

Развёртки стен Г1, Г2. Прихожая (пом. 5)

Прихожая (пом. 5) · вид изнутри помещения · размеры в мм, отметки в м от ±0,000 (чистый пол 1-го этажа)


ПРЕДВАРИТЕЛЬНО · не для производства работ · открыто пунктов: 11 (реестр — л. 7–9)

Развёртка стены Г1

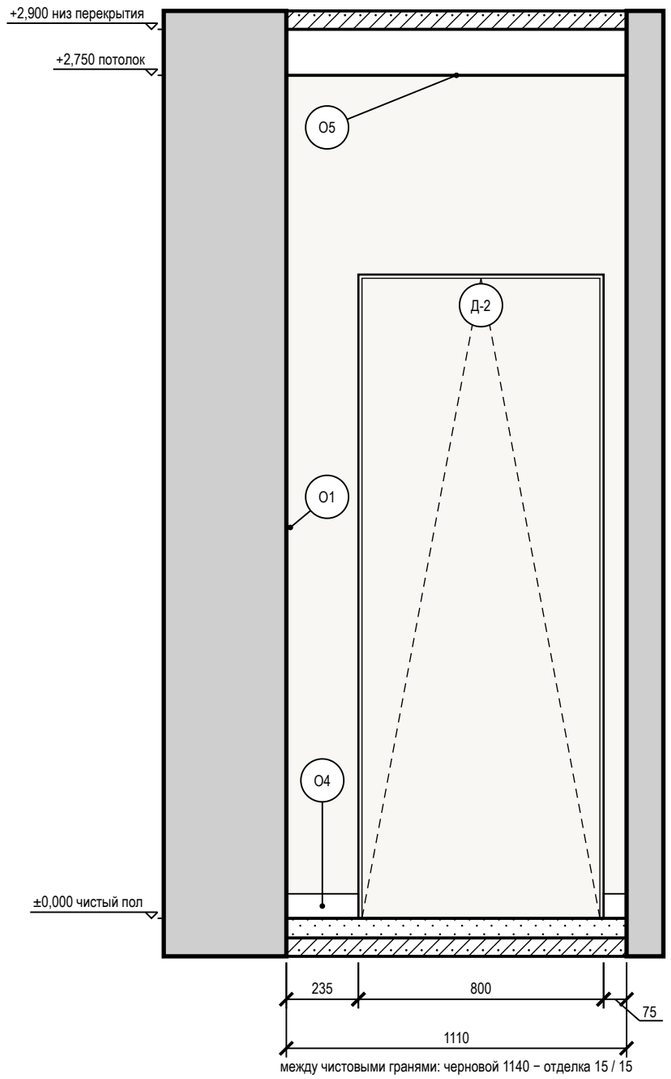


между чистовыми гранями: черновой 1140 − отделка 15 / 15

Развёртка стены Г2

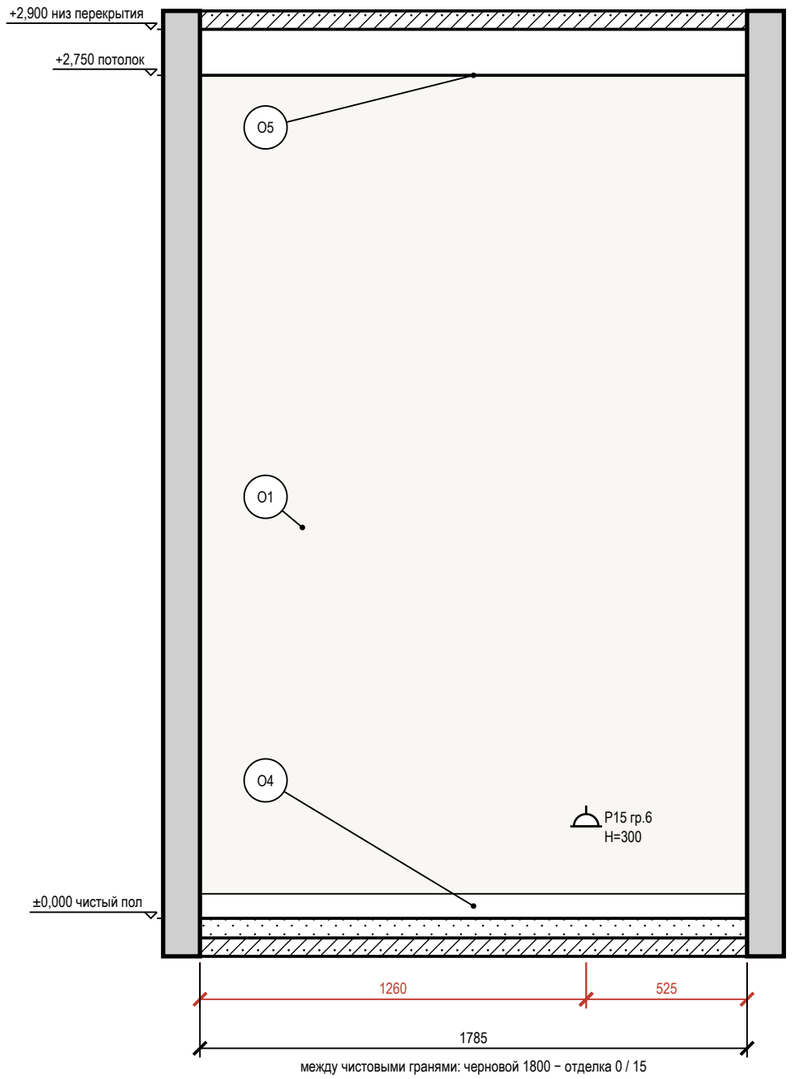

между чистовыми гранями: черновой 1800 − отделка 0 / 15

Схема развёрток (М 1:100)

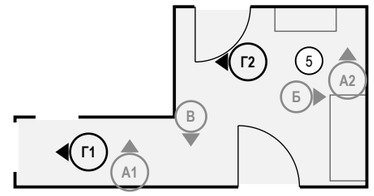

Условные обозначения

- розетка с заземляющим контактом; у знака — марка, ×N постов в рамке, гр. — группа щита, Н — высота оси, мм
- привязки точек и выводов от угла и от пола, мм
- мебель и приборы — фасад по расстановке (условно)
- дверь скрытого монтажа: полотно в плоскости стены (узел — на листе узлов)
- стены и перекрытия в сечении
- окраска: тон — цвет по коду производителя (условно)
- О1 — марка отделки по реестру отделки альбома
- А — марка развёртки: буква стены, стрелка — взгляд

Ведомость отделки (на листе)

Марка	Поверхность	Материал, изделие	Цвет, код	Кол.
О1	стены	окраска, Tikkurila, матовая, подготовка Q3	Tikkurila G503 «Calla»	6,3 м²
О4	плинтус	плинтус МДФ, h 80 мм, аналог: плинтус МДФ под покраску 80×16	Tikkurila G503 «Calla»	2,1 м
О5	потолок	окраска, Little Greene Absolute Matt, глубокоматовая, подготовка Q3	Little Greene No. 222 «Loft White»	12,2 м²

Допущения и предложения на листе

Основа листа: взаимное расположение помещений, контур дома 9600 × 8000 и раскладка этажей подобраны проектировщиком под габариты помещений брифа; обмер и проект АР — задание (К-1); высота потолка 2900 мм — по брифу, не замерена; перекрытие 330 мм и отметка 2-го этажа +3,230 приняты; проект КР — задание (К-2); наружные стены 400 мм, перегородки 120 мм приняты (в брифе толщин нет) (К-1); разрешённая мощность 15 кВт принята по типовым ТУ для частного дома (К-4); подрайон климата не задан — принят не северный (жилые от 2,5 м) (К-7).
Знак «*» — принято, не замерено и не подтверждено (замерить на объекте): К-1: дверь пом. 5 (стена В) — входная дверь: место и ширина проёма приняты проектировщиком по брифу (без плана дома), не замерены; дверь пом. 5 (стена А) — проём: место и ширина приняты проектировщиком по брифу (раскладка этажей — К-1), не замерены.
См. лист открытых вопросов (лист 7, записи К-1, К-2, К-4; лист 8, запись К-7).

Примечания

1. Развёртки — вид на стену изнутри помещения, по часовой стрелке; расположение — на схеме листа и на листе 116; размеры — в мм по чистовым поверхностям; отметки — в м от ±0,000 (чистый пол 1-го этажа); высоты Н — от чистого пола помещения до оси изделия, у декора — до центра.
2. Красная цепочка — привязки электроточек и выводов по осям от угла чистовых стен; высота Н — у знака, от чистого пола до оси; высоты мебели, проёмов и границ отделки — колонкой отметок слева. Стена с 5 и более точками или с мелкими звеньями привязок показана двумя видами: архитектурная развёртка (мебель, отделка, проёмы, высоты) и вид «Привязки» на отдельном листе — точки и выводы с марками, одна цепочка по осям и таблица привязок (каждая точка — строка).
3. У знака электроточки: марка (Р — розетка, S — выключатель, Св — светильник, ЭВ — вывод кабеля), ×N — число постов в рамке, гр. — группа щита, Н — высота оси от чистого пола, мм; группы по клавишам выключателя — на листе выключателей.
4. Схема мебели, приборов и декора не является технической документацией для производства мебели; габариты — по паспортам изделий.
5. Двери скрытого монтажа — полотно в плоскости стены, отделка стены по полотну, плинтус прерывается у короба (узел — на листе узлов).

1000 мм · печать 1:1

Изм.	Кол.уч	Лист	№ док.	Подп.	Дата
Разраб.		Кырлан А.С.			04.11.26
Пров.					
ГИП					
Н. контр.					
Утв.					

ГД-2026-012-АИ

Дом 120 м²

Общая площадь 147,36* м² · * размеры приняты, не замерены (реестр — л. 7–9, К-1)

Дизайн-проект интерьера	Стадия	Лист	Листов
	РП	142	175
Развёртки стен Г1, Г2. Прихожая (пом. 5) М 1:20	**Кырлан Александр Сергеевич**		


выпуск 04.11.2026 № 4dfa962484 · стр. 146 из 180

Развёртка стены А. Спальня родителей (пом. 6)

Спальня родителей (пом. 6) · вид изнутри помещения · размеры в мм, отметки в м от ±0,000 (чистый пол 1-го этажа)


ПРЕДВАРИТЕЛЬНО · не для производства работ · открыто пунктов: 11 (реестр — л. 7–9)

Развёртка стены А

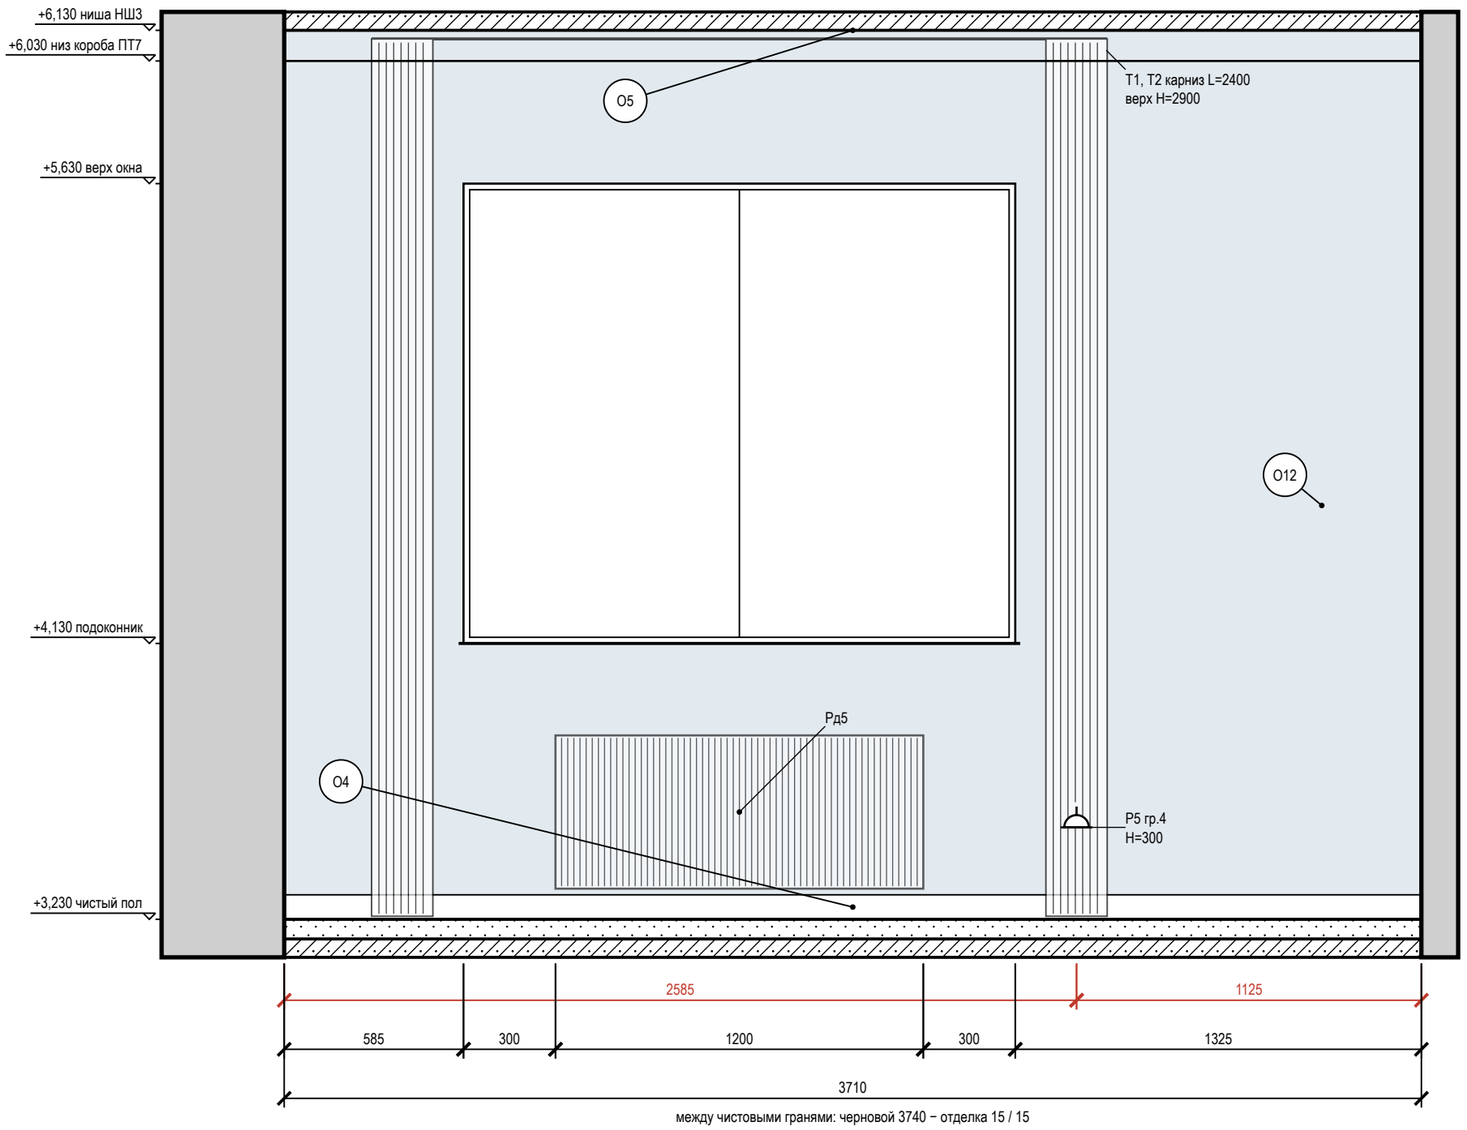

между чистовыми гранями: черновой 3740 − отделка 15 / 15

Схема развёрток (М 1:100)

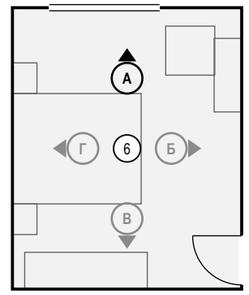

Условные обозначения

- розетка с заземляющим контактом; у знака — марка, ×N — постов в рамке, гр. — группа щита, Н — высота оси, мм
- привязки точек и выводов от угла и от пола, мм
- мебель и приборы — фасад по расстановке (условно)
- карниз (шина) и шторы в собранном виде: марка Т, длина L, верх Н
- окно: проём, рама, подоконник
- радиатор отопления; марка — по плану отопления
- стены и перекрытия в сечении
- окраска: тон — цвет по коду производителя (условно)
- О1 — марка отделки по реестру отделки альбома
- А — марка развёртки: буква стены, стрелка — взгляд

Ведомость отделки (на листе)

Марка	Поверхность	Материал, изделие	Цвет, код	Кол.
О4	плинтус	плинтус МДФ, h 80 мм, аналог: плинтус МДФ под покраску 80×16	Tikkurila G503 «Calla»	3,7 м
О5	потолок	окраска, Little Greene Absolute Matt, глубокоматовая, подготовка Q3	Little Greene No. 222 «Loft White»	17,2 м²
О12	акцентная стена	окраска, Farrow & Ball Modern Emulsion, матовая, подготовка Q3	Farrow & Ball No. 89 «Lulworth Blue — светлая морская лазурь»	8,1 м²

Допущения и предложения на листе

Основа листа: взаимное расположение помещений, контур дома 9600 × 8000 и раскладка этажей подобраны проектировщиком под габариты помещений брифа; обмер и проект АР — задание (К-1); высота потолка 2900 мм — по брифу, не замерена; перекрытие 330 мм и отметка 2-го этажа +3,230 приняты; проект КР — задание (К-2); наружные стены 400 мм, перегородки 120 мм приняты (в брифе толщин нет) (К-1); разрешённая мощность 15 кВт принята по типовым ТУ для частного дома (К-4); подрайон климата не задан — принят не северный (жилые от 2,5 м) (К-7).

Знак «*» — принято, не замерено и не подтверждено (замерить на объекте): К-1: окно пом. 6 (стена А) — окно: место, ширина, высота и подоконник приняты по брифу, стена — по раскладке проектировщика (К-1), не замерены; дверь пом. 6 (стена Б) — проём: место и ширина приняты проектировщиком по брифу (раскладка этажей — К-1), не замерены; К-2: отметка чистого пола этажа «2-й этаж» +3,230 — отметка чистого пола 2-го этажа +3,230 принята: высота потолка 2900 по брифу + перекрытие с полом 330 (конструкция перекрытия не задана; проект КР — задание).

См. лист открытых вопросов (лист 7, записи К-1, К-2, К-4; лист 8, запись К-7).

Примечания

1. Развёртки — вид на стену изнутри помещения, по часовой стрелке; расположение — на схеме листа и на листе 117; размеры — в мм по чистовым поверхностям; отметки — в м от ±0,000 (чистый пол 1-го этажа); высоты Н — от чистого пола помещения до оси изделия, у декора — до центра.
2. Красная цепочка — привязки электроточек и выводов по осям от угла чистовых стен; высота Н — у знака, от чистого пола до оси; высоты мебели, проёмов и границ отделки — колонкой отметок слева. Стена с 5 и более точками или с мелкими звеньями привязок показана двумя видами: архитектурная развёртка (мебель, отделка, проёмы, высоты) и вид «Привязки» на отдельном листе — точки и выводы с марками, одна цепочка по осям и таблица привязок (каждая точка — строка).
3. У знака электроточки: марка (Р — розетка, S — выключатель, Св — светильник, ЭВ — вывод кабеля), ×N — число постов в рамке, гр. — группа щита, Н — высота оси от чистого пола, мм; группы по клавишам выключателя — на листе выключателей.
4. Схема мебели, приборов и декора не является технической документацией для производства мебели; габариты — по паспортам изделий.
5. Карнизы (шины) — по ведомости текстиля декоратора: длина L и верх Н на развёртке — те же числа, что в ведомости; крепление — до окраски потолка.
6. Потолок — у каждой стены свой, по плану потолков (НШ3, ПТ7); ступени — зоной, кромка короба перед нишей — тонкой линией; в поле потолка: ПТ6 +5,880.
7. Линии узора (швы плитки, складки штор, рёбра радиаторов) прерываются у знаков и выносок — просвет между линиями не менее 0,7 мм.

1000 мм · печать 1:1

Изм.	Кол.уч	Лист	№ док.	Подп.	Дата
Разраб.		Кырлан А.С.			04.11.26
Пров.					
ГИП					
Н. контр.					
Утв.					

ГД-2026-012-АИ

Дом 120 м²

Общая площадь 147,36* м² · * размеры приняты, не замерены (реестр — л. 7–9, К-1)

Дизайн-проект интерьера

Стадия	Лист	Листов
РП	143	175

Развёртка стены А. Спальня родителей (пом. 6)

М 1:20

Кырлан Александр Сергеевич


выпуск 04.11.2026 № 4dfa962484 · стр. 147 из 180

Развёртка стены Б. Спальня родителей (пом. 6)

Спальня родителей (пом. 6) · вид изнутри помещения · размеры в мм, отметки в м от ±0,000 (чистый пол 1-го этажа)

ПРЕДВАРИТЕЛЬНО · не для производства работ · открыто пунктов: 11 (реестр — л. 7–9)

Развёртка стены Б

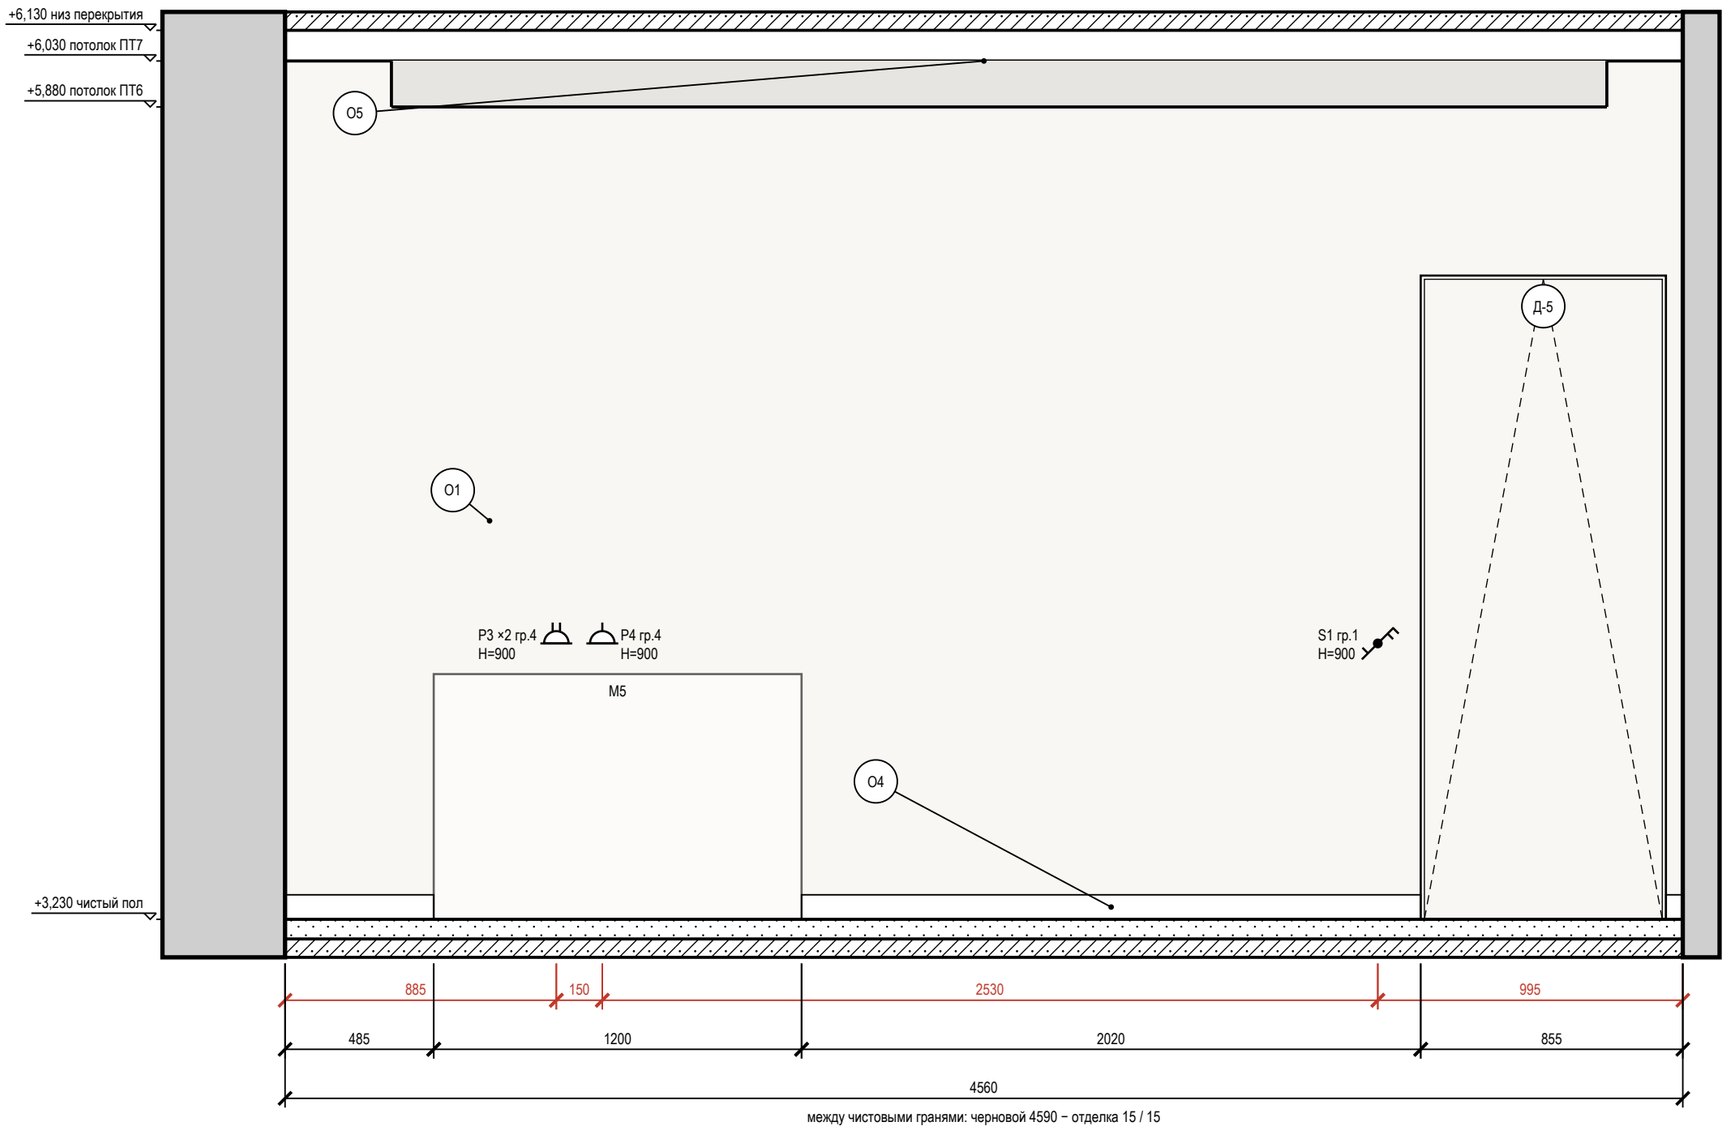

между чистовыми гранями: черновой 4590 − отделка 15 / 15


Допущения и предложения на листе. Основа листа: взаимное расположение помещений, контур дома 9600 × 8000 и раскладка этажей подобраны проектировщиком под габариты помещений брифа; обмер и проект АР — задание (К-1); высота потолка 2900 мм — по брифу, не замерена; перекрытие 330 мм и отметка 2-го этажа +3,230 приняты; проект КР — задание (К-2); наружные стены 400 мм, перегородки 120 мм приняты (в брифе толщин нет) (К-1); разрешённая мощность 15 кВт принята по типовым ТУ для частного дома (К-4); подрайон климата не задан — принят не северный (жилые от 2,5 м) (К-7). Знак «*» — принято, не замерено (замерить): К-1: окно пом. 6 (стена А), дверь пом. 6 (стена Б); К-2: отметка чистого пола этажа «2-й этаж» +3,230. См. лист открытых вопросов (лист 7, записи К-1, К-2, К-4; лист 8, запись К-7).

Примечания

1. Развёртки — вид на стену изнутри помещения, по часовой стрелке; расположение — на схеме листа и на листе 117; размеры — в мм по чистовым поверхностям; отметки — в м от ±0,000 (чистый пол 1-го этажа); высоты Н — от чистого пола помещения до оси изделия, у декора — до центра.
2. Красная цепочка — привязки электроточек и выводов по осям от угла чистовых стен; высота Н — у знака, от чистого пола до оси; высоты мебели, проёмов и границ отделки — колонкой отметок слева. Стена с 5 и более точками или с мелкими звеньями привязок показана двумя видами: архитектурная развёртка (мебель, отделка, проёмы, высоты) и вид «Привязки» на отдельном листе — точки и выводы с марками, одна цепочка по осям и таблица привязок (каждая точка — строка).
3. У знака электроточки: марка (Р — розетка, S — выключатель, Св — светильник, ЭВ — вывод кабеля), ×N — число постов в рамке, гр. — группа щита, Н — высота оси от чистого пола, мм; группы по клавишам выключателя — на листе выключателей.
4. Схема мебели, приборов и декора не является технической документацией для производства мебели; габариты — по паспортам изделий.
5. Двери скрытого монтажа — полотно в плоскости стены, отделка стены по полотну, плинтус прерывается у короба (узел — на листе узлов).
6. Потолок — у каждой стены свой, по плану потолков (ПТ7, ПТ6); ступени — зоной, кромка короба перед нишей — тонкой линией.

1000 мм · печать 1:1

Схема развёрток (М 1:100)

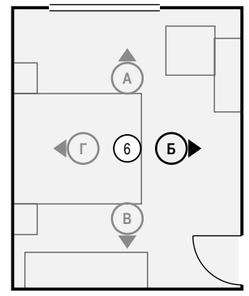

Условные обозначения

- розетка с заземляющим контактом; у знака — марка, ×N постов в рамке, гр. — группа щита, Н — высота оси, мм
- выключатель одноклавишный
- выключатель двухклавишный (флажков — по числу клавиш)
- выключатель с проходной или перекрёстной клавишей (обратный флажок); тип клавиши — в подписи
- привязки точек и выводов от угла и от пола, мм
- мебель и приборы — фасад по расстановке (условно)
- дверь скрытого монтажа: полотно в плоскости стены (узел — на листе узлов)
- стены и перекрытия в сечении
- окраска: тон — цвет по коду производителя (условно)
- О1 — марка отделки по реестру отделки альбома
- А — марка развёртки: буква стены, стрелка — взгляд

Изм.	Кол.уч	Лист	№ док.	Подп.	Дата
Разраб.		Кырлан А.С.			04.11.26
Пров.					
ГИП					
Н. контр.					
Утв.					

ГД-2026-012-АИ

Дом 120 м²

Общая площадь 147,36* м² · * размеры приняты, не замерены (реестр — л. 7–9, К-1)

Дизайн-проект интерьера	Стадия	Лист	Листов
	РП	144	175

Развёртка стены Б. Спальня родителей (пом. 6)

М 1:20


Кырлан Александр Сергеевич

Развёртка стены В. Спальня родителей (пом. 6)

Спальня родителей (пом. 6) · вид изнутри помещения · размеры в мм, отметки в м от ±0,000 (чистый пол 1-го этажа)


ПРЕДВАРИТЕЛЬНО · не для производства работ · открыто пунктов: 11 (реестр — л. 7–9)

Развёртка стены В

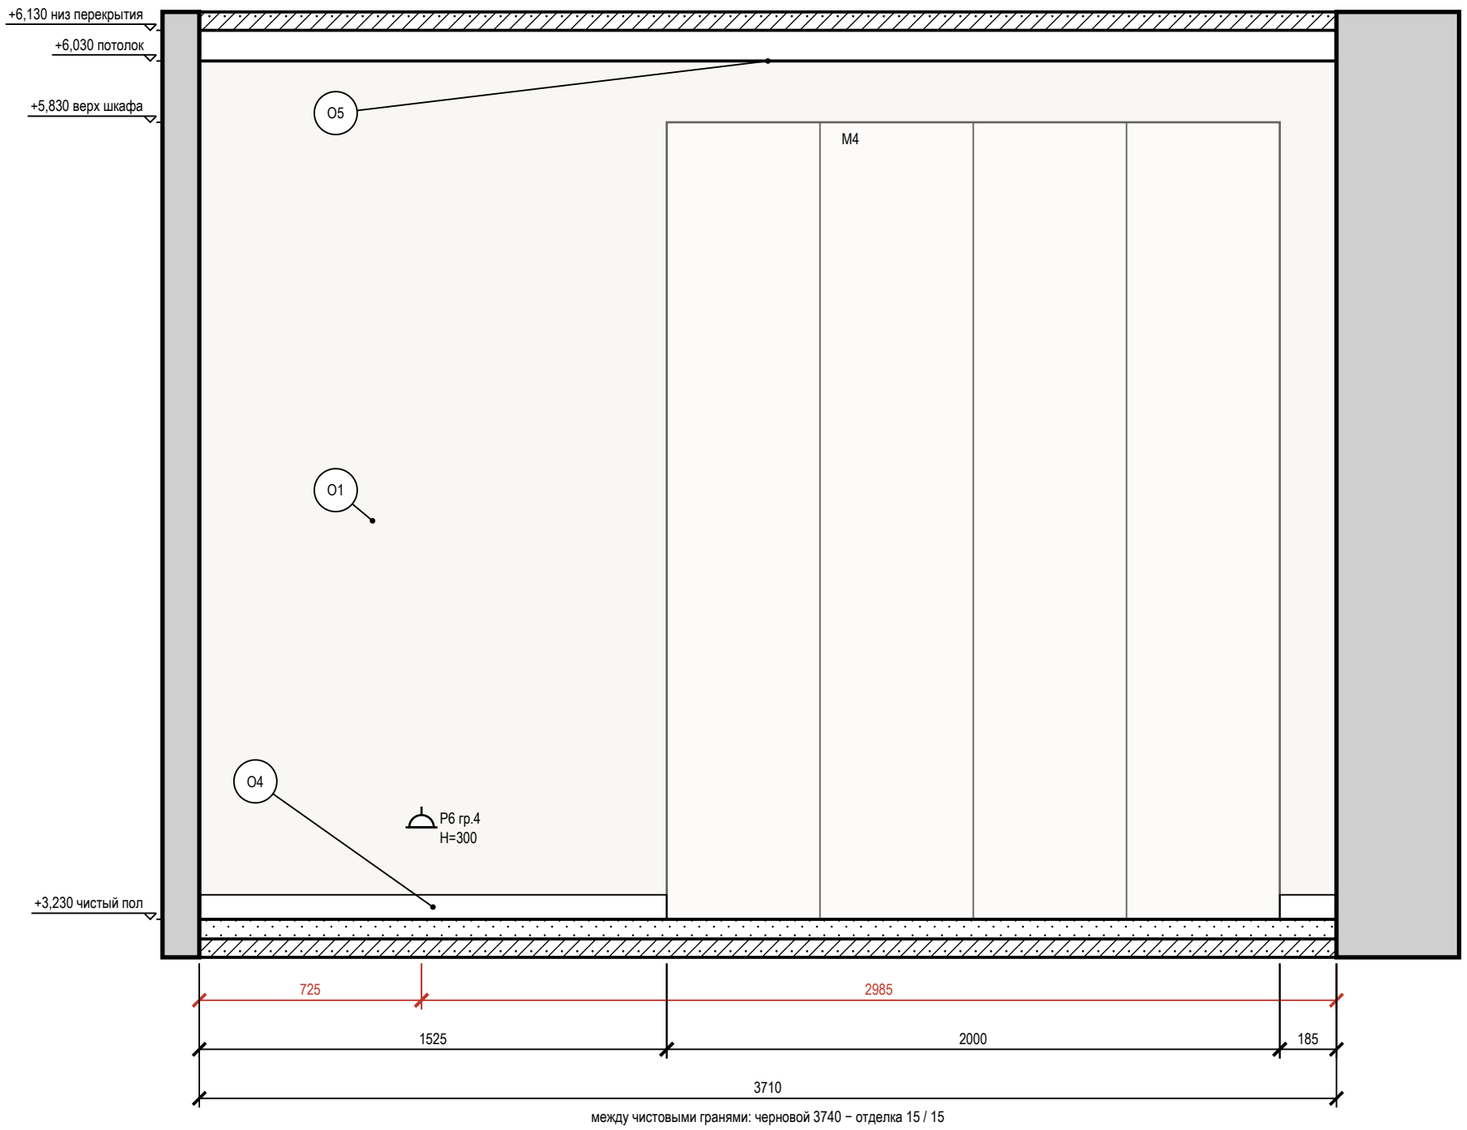

между чистовыми гранями: черновой 3740 − отделка 15 / 15

Схема развёрток (М 1:100)

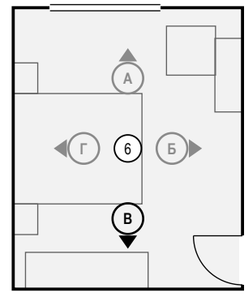

Условные обозначения

- розетка с заземляющим контактом; у знака — марка, ×N постов в рамке, гр. — группа щита, Н — высота оси, мм
- привязки точек и выводов от угла и от пола, мм
- мебель и приборы — фасад по расстановке (условно)
- стены и перекрытия в сечении
- окраска: тон — цвет по коду производителя (условно)
- О1 — марка отделки по реестру отделки альбома
- А — марка развёртки: буква стены, стрелка — взгляд

Ведомость отделки (на листе)

Марка	Поверхность	Материал, изделие	Цвет, код	Кол.
О1	стены	окраска, Tikkurila, матовая, подготовка Q3	Tikkurila G503 «Calla»	10,4 м²
О4	плинтус	плинтус МДФ, h 80 мм, аналог: плинтус МДФ под покраску 80×16	Tikkurila G503 «Calla»	1,7 м
О5	потолок	окраска, Little Greene Absolute Matt, глубокоматовая, подготовка Q3	Little Greene No. 222 «Loft White»	17,2 м²

Допущения и предложения на листе. Основа листа: взаимное расположение помещений, контур дома 9600 × 8000 и раскладка этажей подобраны проектировщиком под габариты помещений брифа; обмер и проект АР — задание (К-1); высота потолка 2900 мм — по брифу, не замерена; перекрытие 330 мм и отметка 2-го этажа +3,230 приняты; проект КР — задание (К-2); наружные стены 400 мм, перегородки 120 мм приняты (в брифе толщин нет) (К-1); разрешённая мощность 15 кВт принята по типовым ТУ для частного дома (К-4); подрайон климата не задан — принят не северный (жилые от 2,5 м) (К-7). Знак «*» — принято, не замерено (замерить): К-1: окно пом. 6 (стена А), дверь пом. 6 (стена Б); К-2: отметка чистого пола этажа «2-й этаж» +3,230. См. лист открытых вопросов (лист 7, записи К-1, К-2, К-4; лист 8, запись К-7).

Примечания

1. Развёртки — вид на стену изнутри помещения, по часовой стрелке; расположение — на схеме листа и на листе 117; размеры — в мм по чистовым поверхностям; отметки — в м от ±0,000 (чистый пол 1-го этажа); высоты Н — от чистого пола помещения до оси изделия, у декора — до центра.
2. Красная цепочка — привязки электроточек и выводов по осям от угла чистовых стен; высота Н — у знака, от чистого пола до оси; высоты мебели, проёмов и границ отделки — колонкой отметок слева. Стена с 5 и более точками или с мелкими звеньями привязок показана двумя видами: архитектурная развёртка (мебель, отделка, проёмы, высоты) и вид «Привязки» на отдельном листе — точки и выводы с марками, одна цепочка по осям и таблица привязок (каждая точка — строка).
3. У знака электроточки: марка (Р — розетка, S — выключатель, Св — светильник, ЭВ — вывод кабеля), ×N — число постов в рамке, гр. — группа щита, Н — высота оси от чистого пола, мм; группы по клавишам выключателя — на листе выключателей.
4. Схема мебели, приборов и декора не является технической документацией для производства мебели; габариты — по паспортам изделий.
5. Потолок — у каждой стены свой, по плану потолков (ПТ7); ступени — зоной, кромка короба перед нишей — тонкой линией; в поле потолка: ПТ6 +5,880.

1000 мм · печать 1:1

Изм.	Кол.уч	Лист	№ док.	Подп.	Дата
Разраб.		Кырлан А.С.			04.11.26
Пров.					
ГИП					
Н. контр.					
Утв.					

ГД-2026-012-АИ

Дом 120 м²

Общая площадь 147,36* м² · * размеры приняты, не замерены (реестр — л. 7–9, К-1)

Дизайн-проект интерьера	Стадия	Лист	Листов
	РП	145	175
Развёртка стены В. Спальня родителей (пом. 6) М 1:20	**Кырлан Александр Сергеевич**		

выпуск 04.11.2026 № 4dfa962484 · стр. 149 из 180

Развёртка стены Г. Спальня родителей (пом. 6)

Спальня родителей (пом. 6) · вид изнутри помещения · размеры в мм, отметки в м от ±0,000 (чистый пол 1-го этажа)

ПРЕДВАРИТЕЛЬНО · не для производства работ · открыто пунктов: 11 (реестр — л. 7–9)

Развёртка стены Г


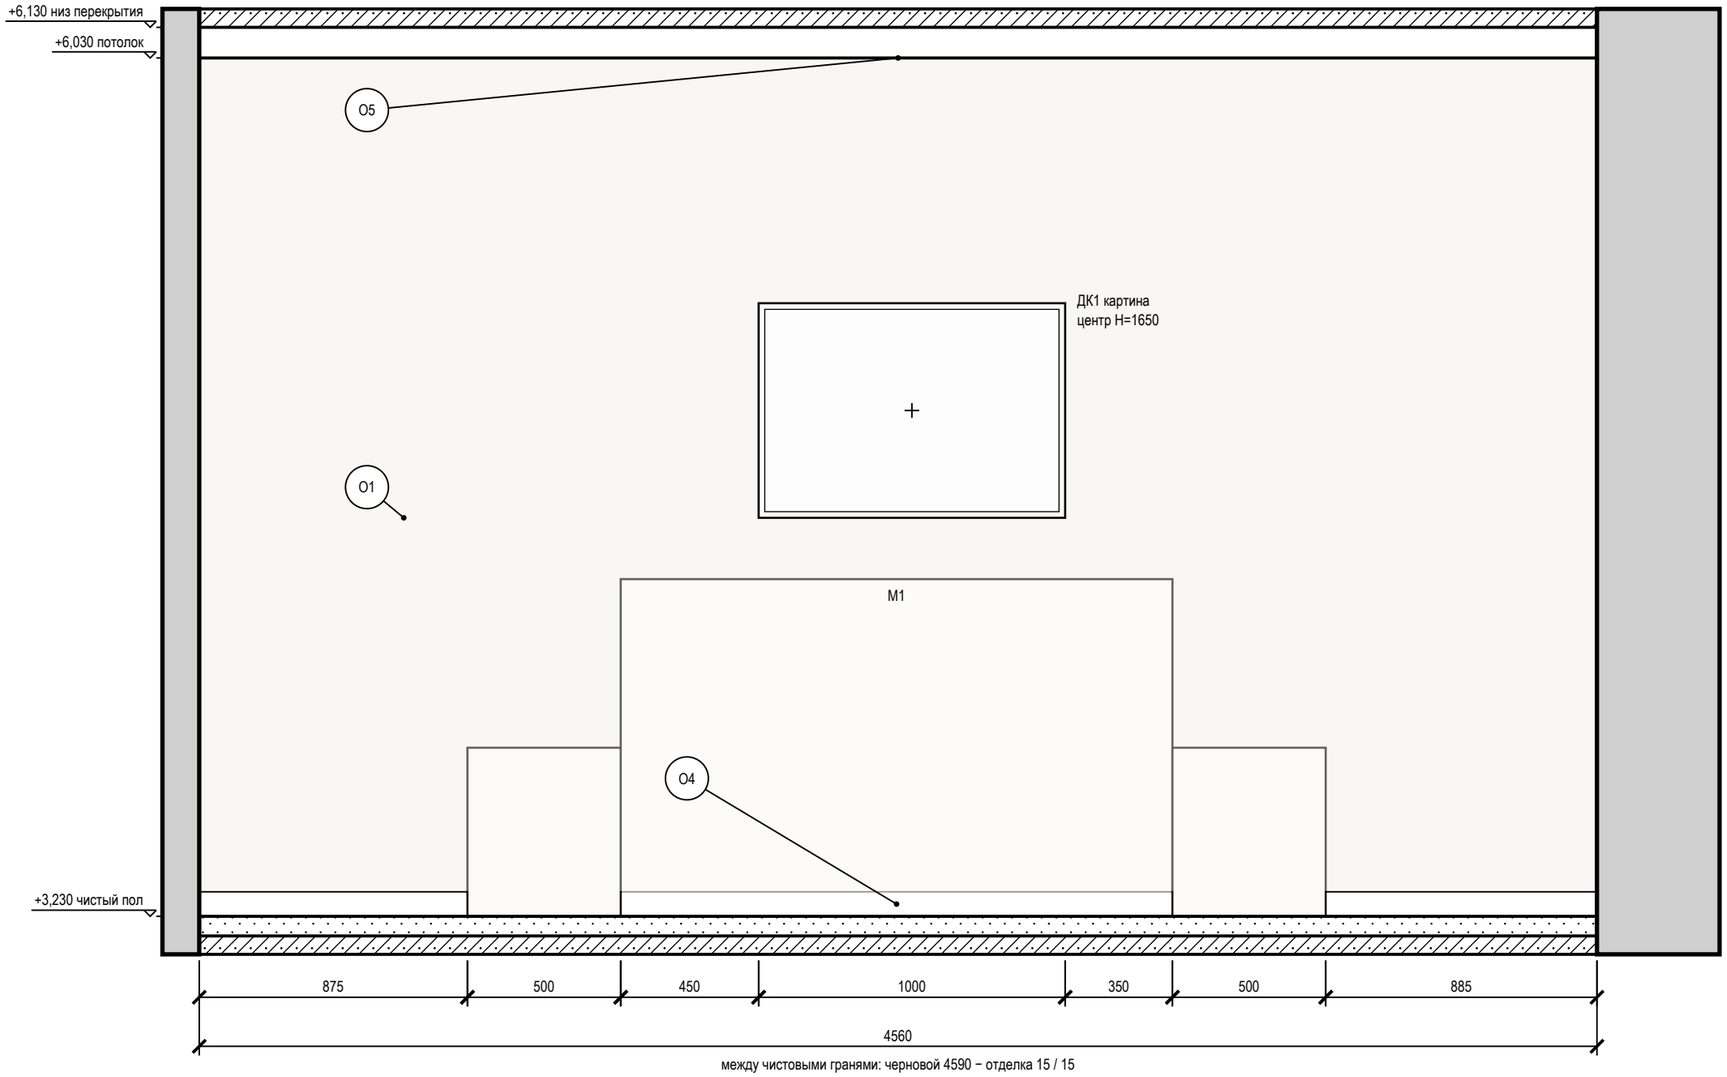


Схема развёрток (М 1:100)

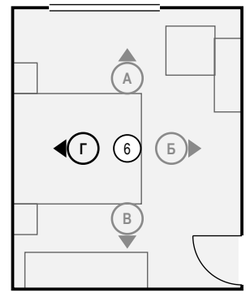

Условные обозначения

- мебель и приборы — фасад по расстановке (условно)
- картина (декор): марка Д, крест — центр, Н — высота центра, мм
- стены и перекрытия в сечении
- окраска: тон — цвет по коду производителя (условно)
- О1 — марка отделки по реестру отделки альбома
- А — марка развёртки: буква стены, стрелка — взгляд

Допущения и предложения на листе

Основа листа: взаимное расположение помещений, контур дома 9600 × 8000 и раскладка этажей подобраны проектировщиком под габариты помещений брифа; обмер и проект АР — задание (К-1); высота потолка 2900 мм — по брифу, не замерена; перекрытие 330 мм и отметка 2-го этажа +3,230 приняты; проект КР — задание (К-2); наружные стены 400 мм, перегородки 120 мм приняты (в брифе толщин нет) (К-1); разрешённая мощность 15 кВт принята по типовым ТУ для частного дома (К-4); подрайон климата не задан — принят не северный (жилые от 2,5 м) (К-7).

Знак «*» — принято, не замерено и не подтверждено (замерить на объекте): К-1: окно пом. 6 (стена А) — окно: место, ширина, высота и подоконник приняты по брифу, стена — по раскладке проектировщика (К-1), не замерены; дверь пом. 6 (стена Б) — проём: место и ширина приняты проектировщиком по брифу (раскладка этажей — К-1), не замерены; К-2: отметка чистого пола этажа «2-й этаж» +3,230 — отметка чистого пола 2-го этажа +3,230 принята: высота потолка 2900 по брифу + перекрытие с полом 330 (конструкция перекрытия не задана; проект КР — задание).

См. лист открытых вопросов (лист 7, записи К-1, К-2, К-4; лист 8, запись К-7).

Примечания

1. Развёртки — вид на стену изнутри помещения, по часовой стрелке; расположение — на схеме листа и на листе 117; размеры — в мм по чистовым поверхностям; отметки — в м от ±0,000 (чистый пол 1-го этажа); высоты Н — от чистого пола помещения до оси изделия, у декора — до центра.
2. Стена Г показана двумя видами: здесь — архитектурная развёртка (мебель, отделка, проёмы, высоты), электроточки и выводы ВК с привязками и таблицей — на листе 147 («Привязки»).
3. Схема мебели, приборов и декора не является технической документацией для производства мебели; габариты — по паспортам изделий.
4. Картины и зеркала крепить к основанию по паспорту изделия (закладные и анкеры — в перечне скрытых работ); крест — ось центра предмета.
5. Потолок — у каждой стены свой, по плану потолков (ПТ7); ступени — зоной, кромка короба перед нишей — тонкой линией; в поле потолка: ПТ6 +5,880.

1000 мм · печать 1:1

Изм.	Кол.уч	Лист	№ док.	Подп.	Дата
Разраб.		Кырлан А.С.			04.11.26
Пров.					
ГИП					
Н. контр.					
Утв.					

ГД-2026-012-АИ

Дом 120 м²

Общая площадь 147,36* м² · * размеры приняты, не замерены (реестр — л. 7–9, К-1)

Дизайн-проект интерьера

Стадия	Лист	Листов
РП	146	175

Развёртка стены Г. Спальня родителей (пом. 6)

М 1:20

Кырлан Александр Сергеевич

выпуск 04.11.2026 № 4dfa962484 · стр. 150 из 180

Привязки электроточек, стена Г. Спальня родителей (пом. 6)

Спальня родителей (пом. 6) · вид изнутри помещения · привязки в мм, отметки в м · к развёртке на листе 146

ПРЕДВАРИТЕЛЬНО · не для производства работ · открыто пунктов: 11 (реестр — л. 7–9)

Развёртка стены Г: электроточки и выводы

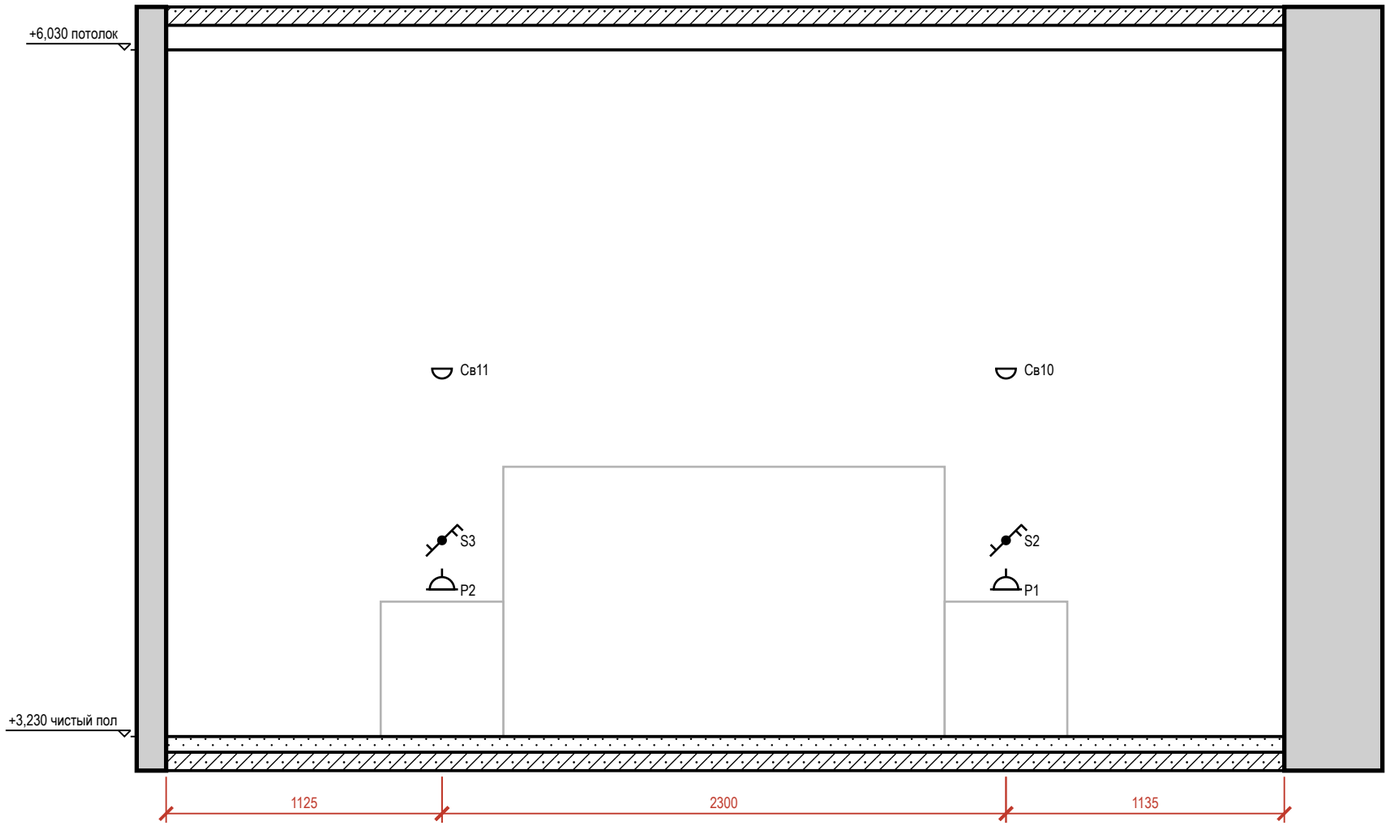



Таблица привязок электроточек и выводов

Марка	Назначение	От угла, мм	Н от пола, мм	Примечание
P2	розетка: у кровати	1125	600	гр. 4
S3	выключатель	1125	800	гр. 1
Св11	светильник настенный	1125	1500	гр. 1
P1	розетка: у кровати	3425	600	гр. 4
S2	выключатель	3425	800	гр. 1
Св10	светильник настенный	3425	1500	гр. 1

Условные обозначения

- розетка с заземляющим контактом; у знака — марка, ×N постов в рамке, гр. — группа щита, Н — высота оси, мм
- выключатель одноклавишный
- выключатель двухклавишный (флажков — по числу клавиш)
- выключатель с проходной или перекрёстной клавишей (обратный флажок); тип клавиши — в подписи
- светильник настенный (бра), Н — высота оси
- привязки точек и выводов от угла и от пола, мм
- марка развёртки: буква стены, стрелка — взгляд

Схема развёрток (М 1:100)

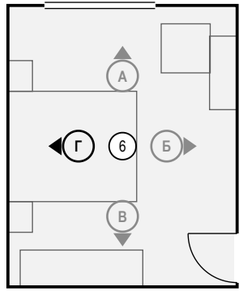

Допущения и предложения на листе

Основа листа: взаимное расположение помещений, контур дома 9600 × 8000 и раскладка этажей подобраны проектировщиком под габариты помещений брифа; обмер и проект АР — задание (К-1); высота потолка 2900 мм — по брифу, не замерена; перекрытие 330 мм и отметка 2-го этажа +3,230 приняты; проект КР — задание (К-2); наружные стены 400 мм, перегородки 120 мм приняты (в брифе толщин нет) (К-1); разрешённая мощность 15 кВт принята по типовым ТУ для частного дома (К-4); подрайон климата не задан — принят не северный (жилые от 2,5 м) (К-7).
Знак «*» — принято, не замерено и не подтверждено (замерить на объекте): К-1: окно пом. 6 (стена А) — окно: место, ширина, высота и подоконник приняты по брифу, стена — по раскладке проектировщика (К-1), не замерены; дверь пом. 6 (стена Б) — проём: место и ширина приняты проектировщиком по брифу (раскладка этажей — К-1), не замерены; К-2: отметка чистого пола этажа «2-й этаж» +3,230 — отметка чистого пола 2-го этажа +3,230 принята: высота потолка 2900 по брифу + перекрытие с полом 330 (конструкция перекрытия не задана; проект КР — задание).
См. лист открытых вопросов (лист 7, записи К-1, К-2, К-4; лист 8, запись К-7).

Примечания

1. Вид «Привязки» стены Г — электроточки и выводы ВК; архитектурная развёртка (мебель, отделка, проёмы, высоты) — на листе 146, расположение — на листе 117. Мебель и приборы — подложкой для ориентира; их марки и обозначения мебели, проёмов и стен — там же.
2. Привязки — в мм: по горизонтали от левого чистового угла стены до оси изделия, Н — от чистого пола до оси; все точки — в таблице привязок. Красная цепочка — привязки по осям; точки ближе 150 мм одна к другой в цепочку не дробятся — их привязки только в таблице.
3. У знака — марка электроточки (Р — розетка, S — выключатель, Св — светильник, ЭВ — вывод кабеля); посты в рамке и группа щита — в графе «Примечание»; группы по клавишам выключателя — на листе выключателей.

1000 мм · печать 1:1

Изм.	Кол.уч	Лист	№ док.	Подп.	Дата
Разраб.		Кырлан А.С.			04.11.26
Пров.					
ГИП					
Н. контр.					
Утв.					

ГД-2026-012-АИ

Дом 120 м²

Общая площадь 147,36* м² · * размеры приняты, не замерены (реестр — л. 7–9, К-1)

Дизайн-проект интерьера

Стадия	Лист	Листов
РП	147	175

Привязки электроточек, стена Г. Спальня родителей (пом. 6)

М 1:25

Кырлан Александр Сергеевич


выпуск 04.11.2026 № 4dfa962484 · стр. 151 из 180

Развёртка стены А. Детская (пом. 7)

Детская (пом. 7) · вид изнутри помещения · размеры в мм, отметки в м от ±0,000 (чистый пол 1-го этажа)


ПРЕДВАРИТЕЛЬНО · не для производства работ · открыто пунктов: 11 (реестр — л. 7–9)

Развёртка стены А

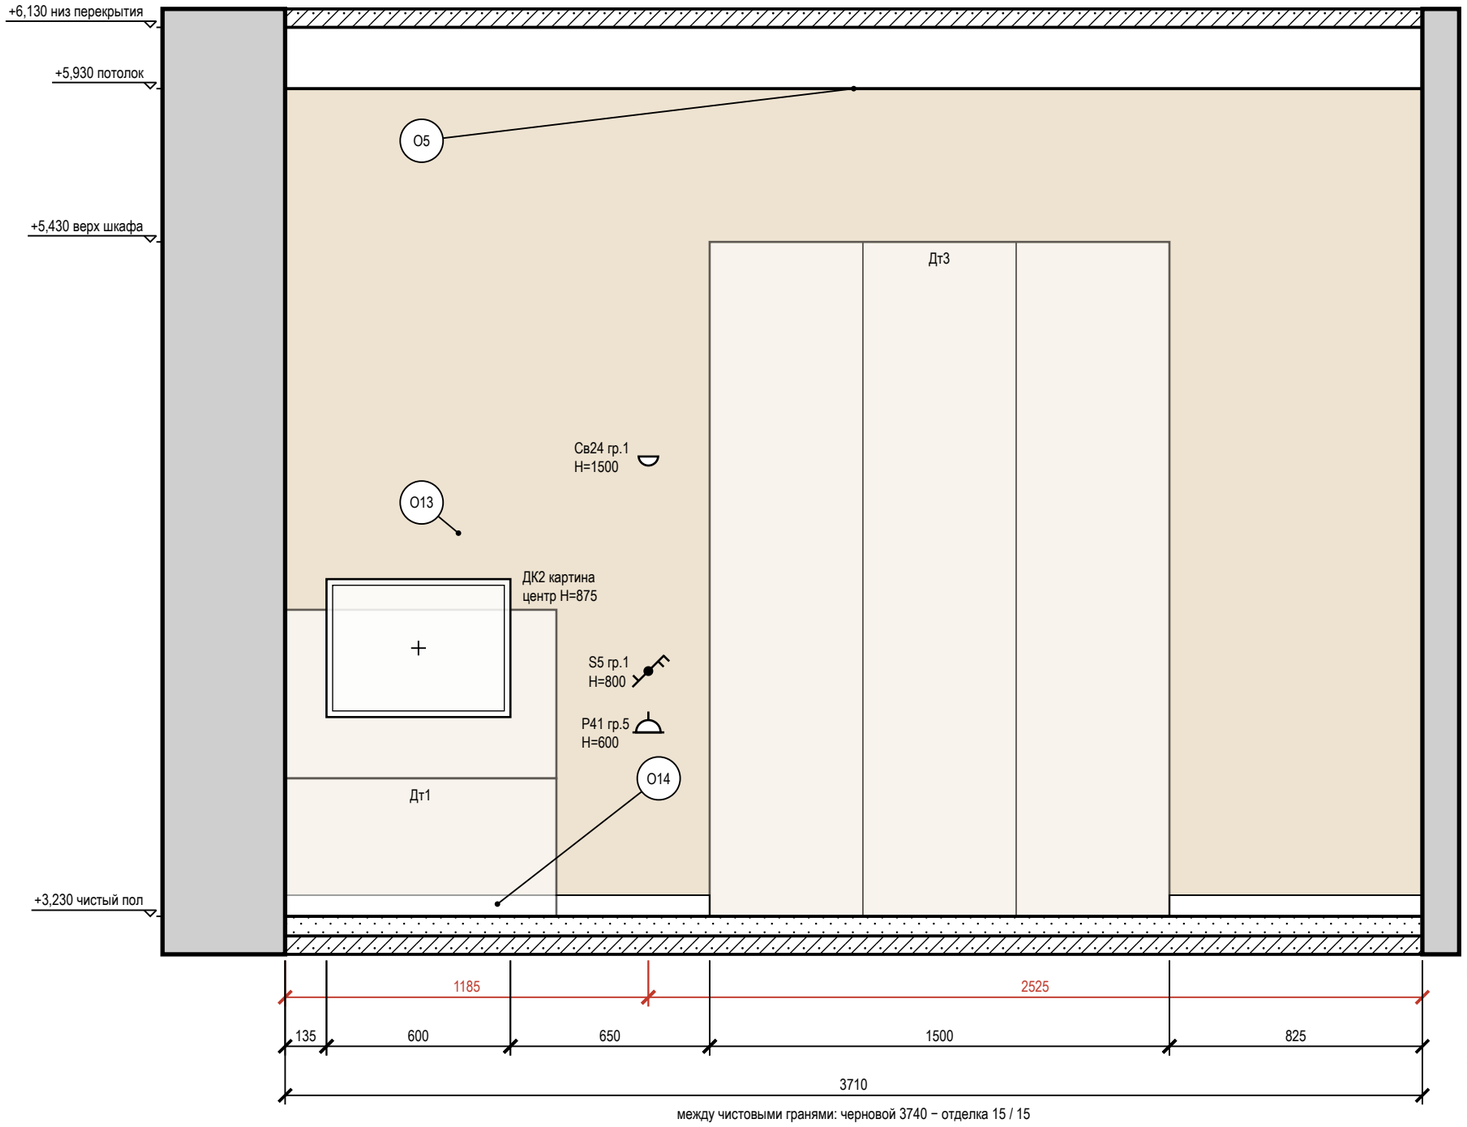

между чистовыми гранями: черновой 3740 − отделка 15 / 15

Схема развёрток (М 1:100)

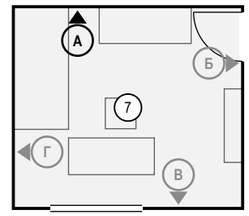

Условные обозначения

- розетка с заземляющим контактом; у знака — марка, ×N — постов в рамке, гр. — группа щита, H — высота оси, мм
- выключатель одноклавишный
- выключатель двухклавишный (флажков — по числу клавиш)
- выключатель с проходной или перекрёстной клавишей (обратный флажок); тип клавиши — в подписи
- светильник настенный (бра), H — высота оси
- привязки точек и выводов от угла и от пола, мм
- мебель и приборы — фасад по расстановке (условно)
- картина (декор): марка Д, крест — центр, H — высота центра, мм
- стены и перекрытия в сечении
- окраска: тон — цвет по коду производителя (условно)
- О1 — марка отделки по реестру отделки альбома
- А — марка развёртки: буква стены, стрелка — взгляд

Ведомость отделки (на листе)

Марка	Поверхность	Материал, изделие	Цвет, код	Кол.
О5	потолок	окраска, Little Greene Absolute Matt, глубокоматовая, подготовка Q3	Little Greene No. 222 «Loft White»	12,3 м²
О13	акцентная стена	окраска, Farrow & Ball, шелковисто-матовая, подготовка Q3	Farrow & Ball No. 66 «India Yellow — охра / горчица итальянских фасадов»	10 м²
О14	плинтус	плинтус МДФ, Orac Decor Contour (Luxxus), h 69 мм, SX165	Tikkurila G503 «Calla»	2,2 м

Допущения и предложения на листе

Основа листа: взаимное расположение помещений, контур дома 9600 × 8000 и раскладка этажей подобраны проектировщиком под габариты помещений брифа; обмер и проект АР — задание (К-1); высота потолка 2900 мм — по брифу, не замерена; перекрытие 330 мм и отметка 2-го этажа +3,230 приняты; проект КР — задание (К-2); наружные стены 400 мм, перегородки 120 мм приняты (в брифе толщин нет) (К-1); разрешённая мощность 15 кВт принята по типовым ТУ для частного дома (К-4); подрайон климата не задан — принят не северный (жилые от 2,5 м) (К-7).

Знак «*» — принято, не замерено и не подтверждено (замерить на объекте): К-1: окно пом. 7 (стена В) — окно: место, ширина, высота и подоконник приняты по брифу, стена — по раскладке проектировщика (К-1), не замерены; дверь пом. 7 (стена Б) — проём: место и ширина приняты проектировщиком по брифу (раскладка этажей — К-1), не замерены; К-2: отметка чистого пола этажа «2-й этаж» +3,230 — отметка чистого пола 2-го этажа +3,230 принята: высота потолка 2900 по брифу + перекрытие с полом 330 (конструкция перекрытия не задана; проект КР — задание).

См. лист открытых вопросов (лист 7, записи К-1, К-2, К-4; лист 8, запись К-7).

Примечания

1. Развёртки — вид на стену изнутри помещения, по часовой стрелке; расположение — на схеме листа и на листе 117; размеры — в мм по чистовым поверхностям; отметки — в м от ±0,000 (чистый пол 1-го этажа); высоты H — от чистого пола помещения до оси изделия, у декора — до центра.
2. Красная цепочка — привязки электроточек и выводов по осям от угла чистовых стен; высота H — у знака, от чистого пола до оси; высоты мебели, проёмов и границ отделки — колонкой отметок слева. Стена с 5 и более точками или с мелкими звеньями привязок показана двумя видами: архитектурная развёртка (мебель, отделка, проёмы, высоты) и вид «Привязки» на отдельном листе — точки и выводы с марками, одна цепочка по осям и таблица привязок (каждая точка — строка).
3. У знака электроточки: марка (Р — розетка, S — выключатель, Св — светильник, ЭВ — вывод кабеля), ×N — число постов в рамке, гр. — группа щита, H — высота оси от чистого пола, мм; группы по клавишам выключателя — на листе выключателей.
4. Схема мебели, приборов и декора не является технической документацией для производства мебели; габариты — по паспортам изделий.
5. Картины и зеркала крепить к основанию по паспорту изделия (закладные и анкеры — в перечне скрытых работ); крест — ось центра предмета.
6. Потолок — у каждой стены свой, по плану потолков (ПТ8); ступени — зоной, кромка короба перед нишей — тонкой линией; в поле потолка: ПТ7 +6,030.

1000 мм · печать 1:1

Изм.	Кол.уч	Лист	№ док.	Подп.	Дата
Разраб.		Кырлан А.С.			04.11.26
Пров.					
ГИП					
Н. контр.					
Утв.					

ГД-2026-012-АИ

Дом 120 м²

Общая площадь 147,36* м² · * размеры приняты, не замерены (реестр — л. 7–9, К-1)

Дизайн-проект интерьера

Стадия	Лист	Листов
РП	148	175

Развёртка стены А. Детская (пом. 7)

М 1:20

Кырлан Александр Сергеевич

выпуск 04.11.2026 № 4dfa962484 · стр. 152 из 180

Развёртка стены Б. Детская (пом. 7)

Детская (пом. 7) · вид изнутри помещения · размеры в мм, отметки в м от ±0,000 (чистый пол 1-го этажа)

ПРЕДВАРИТЕЛЬНО · не для производства работ · открыто пунктов: 11 (реестр — л. 7–9)

Развёртка стены Б


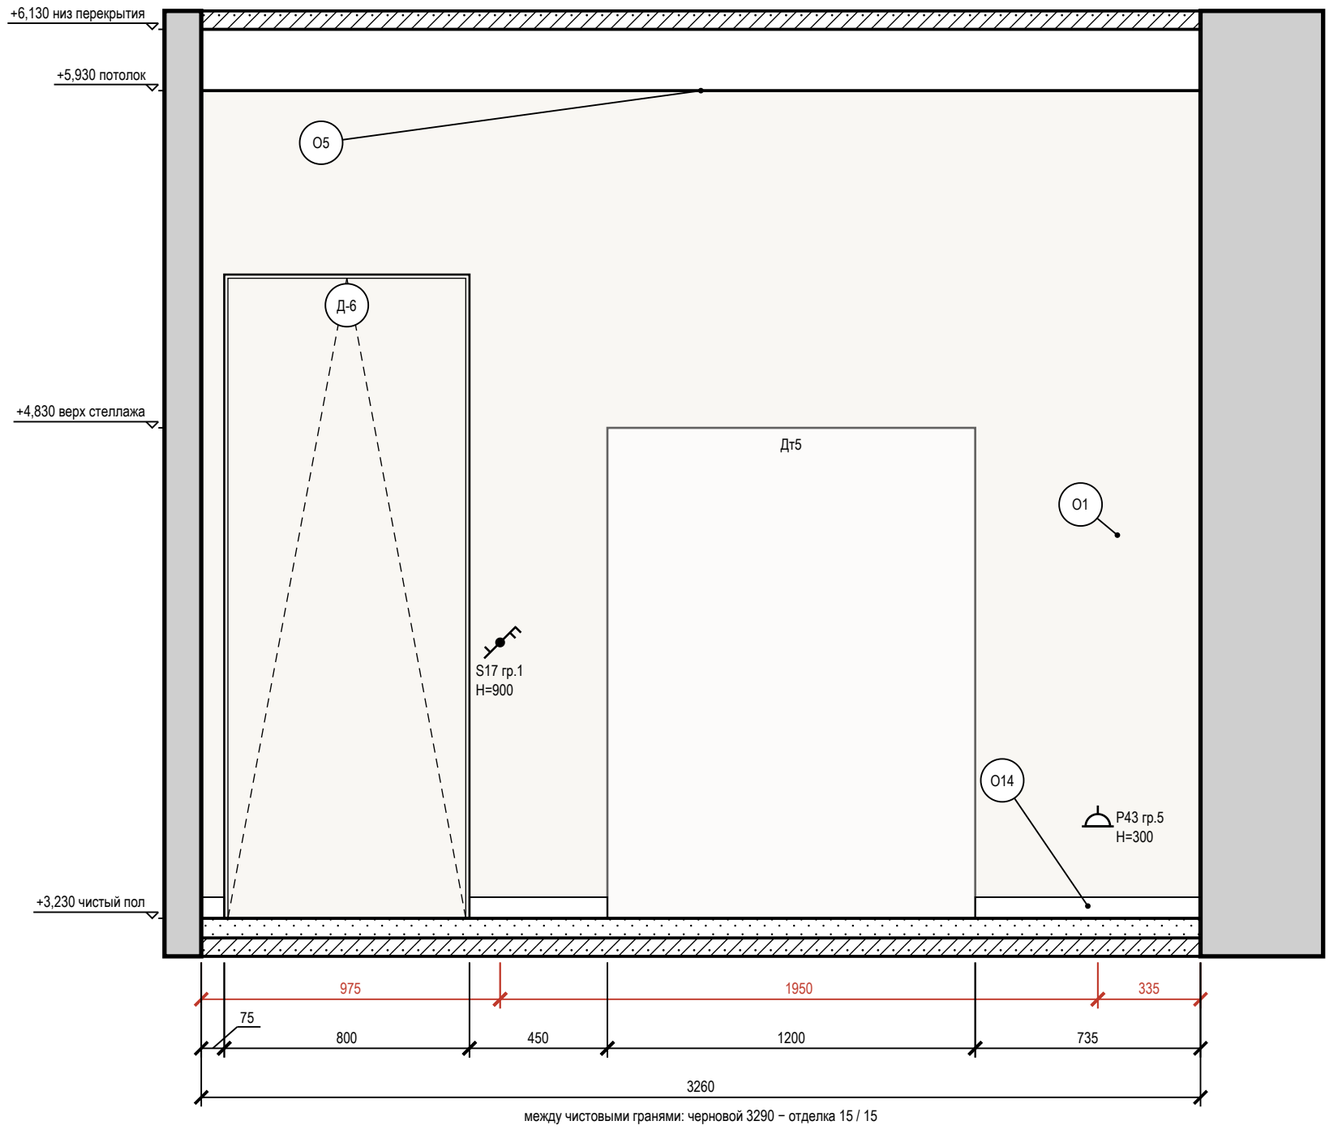


Схема развёрток (М 1:100)

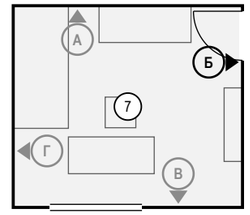

Условные обозначения

- розетка с заземляющим контактом; у знака — марка, ×N постов в рамке, гр. — группа щита, Н — высота оси, мм
- выключатель одноклавишный
- выключатель двухклавишный (флажков — по числу клавиш)
- выключатель с проходной или перекрёстной клавишей (обратный флажок); тип клавиши — в подписи
- привязки точек и выводов от угла и от пола, мм
- мебель и приборы — фасад по расстановке (условно)
- дверь скрытого монтажа: полотно в плоскости стены (узел — на листе узлов)
- стены и перекрытия в сечении
- окраска: тон — цвет по коду производителя (условно)
- О1 — марка отделки по реестру отделки альбома
- А — марка развёртки: буква стены, стрелка — взгляд

Ведомость отделки (на листе)

Марка	Поверхность	Материал, изделие	Цвет, код	Кол.
О1	стены	окраска, Tikkurila, шелковисто-матовая, подготовка Q3	Tikkurila G503 «Calla»	7,1 м²
О5	потолок	окраска, Little Greene Absolute Matt, глубокоматовая, подготовка Q3	Little Greene No. 222 «Loft White»	12,3 м²
О14	плинтус	плинтус МДФ, Orac Decor Contour (Luxxus), h 69 мм, SX165	Tikkurila G503 «Calla»	1,3 м

Допущения и предложения на листе. Основа листа: взаимное расположение помещений, контур дома 9600 × 8000 и раскладка этажей подобраны проектировщиком под габариты помещений брифа; обмер и проект АР — задание (К-1); высота потолка 2900 мм — по брифу, не замерена; перекрытие 330 мм и отметка 2-го этажа +3,230 приняты; проект КР — задание (К-2); наружные стены 400 мм, перегородки 120 мм приняты (в брифе толщин нет) (К-1); разрешённая мощность 15 кВт принята по типовым ТУ для частного дома (К-4); подрайон климата не задан — принят не северный (жилые от 2,5 м) (К-7). Знак «*» — принято, не замерено (замерить): К-1: окно пом. 7 (стена В), дверь пом. 7 (стена Б); К-2: отметка чистого пола этажа «2-й этаж» +3,230. См. лист открытых вопросов (лист 7, записи К-1, К-2, К-4; лист 8, запись К-7).

Примечания

1. Развёртки — вид на стену изнутри помещения, по часовой стрелке; расположение — на схеме листа и на листе 117; размеры — в мм по чистовым поверхностям; отметки — в м от ±0,000 (чистый пол 1-го этажа); высоты Н — от чистого пола помещения до оси изделия, у декора — до центра.
2. Красная цепочка — привязки электроточек и выводов по осям от угла чистовых стен; высота Н — у знака, от чистого пола до оси; высоты мебели, проёмов и границ отделки — колонкой отметок слева. Стена с 5 и более точками или с мелкими звеньями привязок показана двумя видами: архитектурная развёртка (мебель, отделка, проёмы, высоты) и вид «Привязки» на отдельном листе — точки и выводы с марками, одна цепочка по осям и таблица привязок (каждая точка — строка).
3. У знака электроточки: марка (Р — розетка, S — выключатель, Св — светильник, ЭВ — вывод кабеля), ×N — число постов в рамке, гр. — группа щита, Н — высота оси от чистого пола, мм; группы по клавишам выключателя — на листе выключателей.
4. Схема мебели, приборов и декора не является технической документацией для производства мебели; габариты — по паспортам изделий.
5. Двери скрытого монтажа — полотно в плоскости стены, отделка стены по полотну, плинтус прерывается у короба (узел — на листе узлов).
6. Потолок — у каждой стены свой, по плану потолков (ПТ8); ступени — зоной, кромка короба перед нишей — тонкой линией; в поле потолка: ПТ7 +6,030.

1000 мм · печать 1:1

Изм.	Кол.уч	Лист	№ док.	Подп.	Дата
Разраб.		Кырлан А.С.			04.11.26
Пров.					
ГИП					
Н. контр.					
Утв.					

ГД-2026-012-АИ

Дом 120 м²

Общая площадь 147,36* м² · * размеры приняты, не замерены (реестр — л. 7–9, К-1)

Дизайн-проект интерьера	Стадия	Лист	Листов
	РП	149	175

Развёртка стены Б. Детская (пом. 7)

М 1:20

Кырлан Александр Сергеевич


выпуск 04.11.2026 № 4dfa962484 · стр. 153 из 180

Развёртка стены В. Детская (пом. 7)

Детская (пом. 7) · вид изнутри помещения · размеры в мм, отметки в м от ±0,000 (чистый пол 1-го этажа)

ПРЕДВАРИТЕЛЬНО · не для производства работ · открыто пунктов: 11 (реестр — л. 7–9)

Развёртка стены В

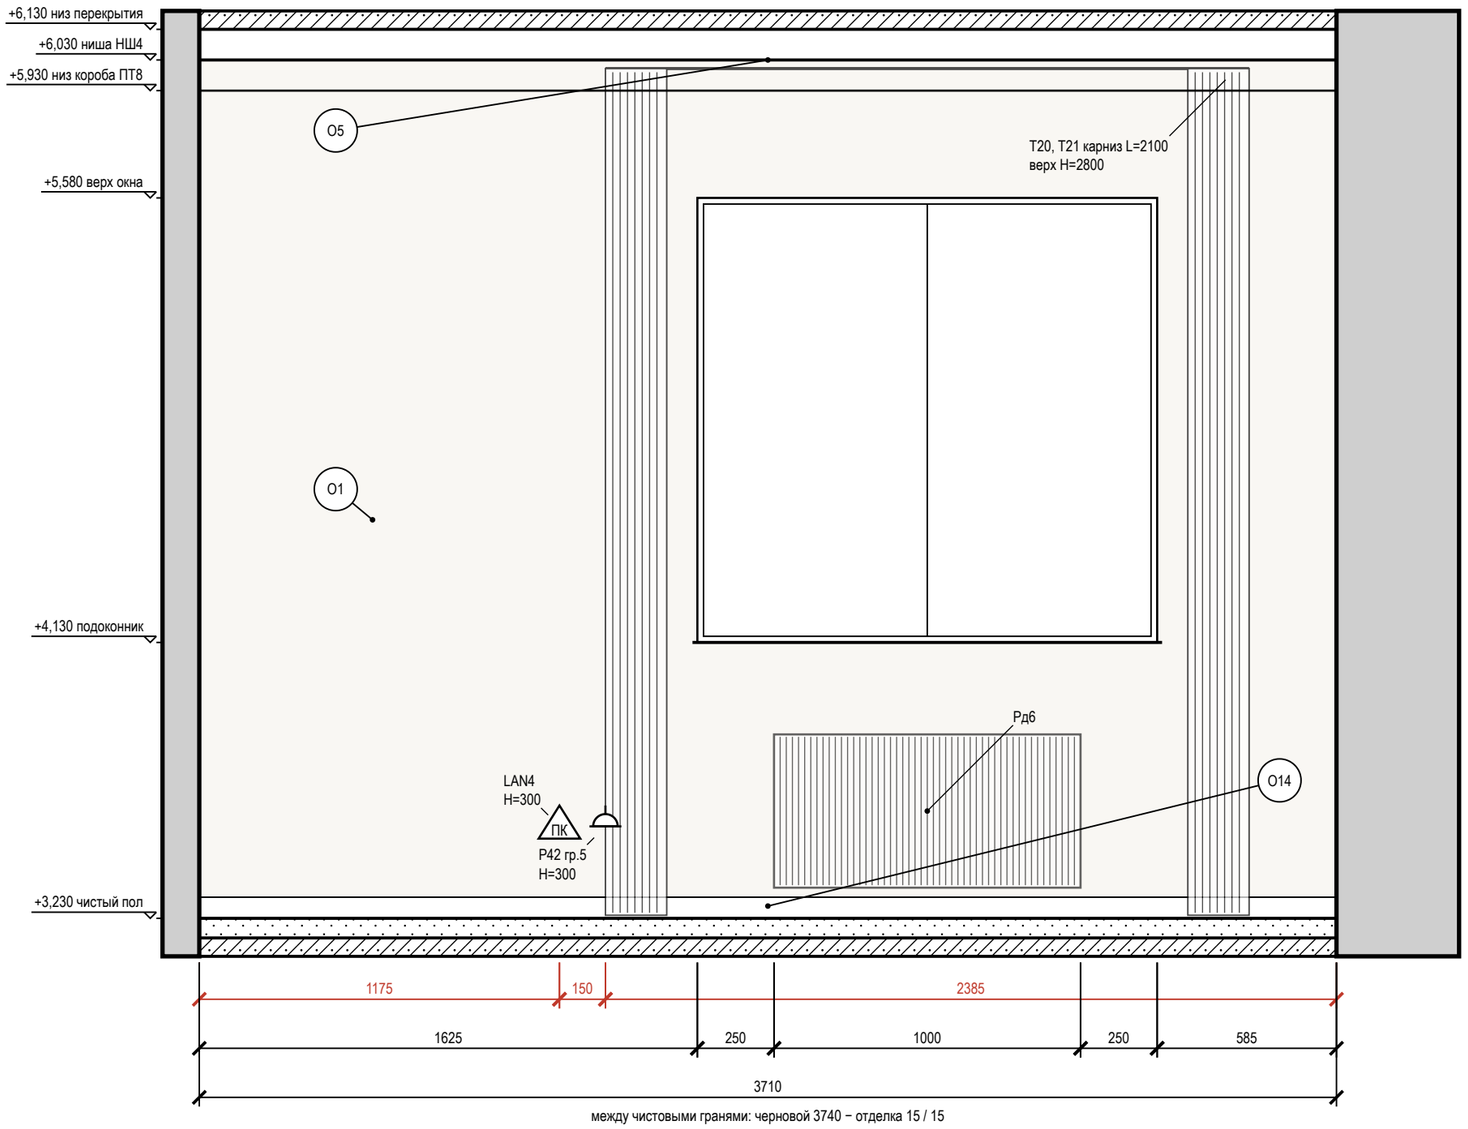


Допущения и предложения на листе. Основа листа: взаимное расположение помещений, контур дома 9600 × 8000 и раскладка этажей подобраны проектировщиком под габариты помещений брифа; обмер и проект АР — задание (К-1); высота потолка 2900 мм — по брифу, не замерена; перекрытие 330 мм и отметка 2-го этажа +3,230 приняты; проект КР — задание (К-2); наружные стены 400 мм, перегородки 120 мм приняты (в брифе толщин нет) (К-1); разрешённая мощность 15 кВт принята по типовым ТУ для частного дома (К-4); подрайон климата не задан — принят не северный (жилые от 2,5 м) (К-7). Знак «*» — принято, не замерено (замерить): К-1: окно пом. 7 (стена В), дверь пом. 7 (стена Б); К-2: отметка чистого пола этажа «2-й этаж» +3,230. См. лист открытых вопросов (лист 7, записи К-1, К-2, К-4; лист 8, запись К-7; лист 9, запись ИЗ-2).

Примечания

1. Развёртки — вид на стену изнутри помещения, по часовой стрелке; расположение — на схеме листа и на листе 117; размеры — в мм по чистовым поверхностям; отметки — в м от ±0,000 (чистый пол 1-го этажа); высоты Н — от чистого пола помещения до оси изделия, у декора — до центра.
2. Красная цепочка — привязки электроточек и выводов по осям от угла чистовых стен; высота Н — у знака, от чистого пола до оси; высоты мебели, проёмов и границ отделки — колонкой отметок слева. Стена с 5 и более точками или с мелкими звеньями привязок показана двумя видами: архитектурная развёртка (мебель, отделка, проёмы, высоты) и вид «Привязки» на отдельном листе — точки и выводы с марками, одна цепочка по осям и таблица привязок (каждая точка — строка).
3. У знака электроточки: марка (Р — розетка, S — выключатель, Св — светильник, ЭВ — вывод кабеля), ×N — число постов в рамке, гр. — группа щита, Н — высота оси от чистого пола, мм; группы по клавишам выключателя — на листе выключателей.
4. Схема мебели, приборов и декора не является технической документацией для производства мебели; габариты — по паспортам изделий.
5. Карнизы (шины) — по ведомости текстиля декоратора: длина L и верх Н на развёртке — те же числа, что в ведомости; крепление — до окраски потолка.
6. Потолок — у каждой стены свой, по плану потолков (НШ4, ПТ8); ступени — зоной, кромка короба перед нишей — тонкой линией; в поле потолка: ПТ7 +6,030.

1000 мм · печать 1:1

Схема развёрток (М 1:100)

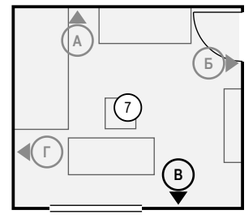

Условные обозначения

- розетка с заземляющим контактом; у знака — марка, ×N постов в рамке, гр. — группа щита, Н — высота оси, мм
- ПК — розетка компьютерная RJ45
- привязки точек и выводов от угла и от пола, мм
- мебель и приборы — фасад по расстановке (условно)
- карниз (шина) и шторы в собранном виде: марка Т, длина L, верх Н
- окно: проём, рама, подоконник
- радиатор отопления; марка — по плану отопления
- стены и перекрытия в сечении
- окраска: тон — цвет по коду производителя (условно)
- О1 — марка отделки по реестру отделки альбома
- А — марка развёртки: буква стены, стрелка — взгляд

Ведомость отделки (на листе)

Марка	Поверхность	Материал, изделие	Цвет, код	Кол.
О1	стены	окраска, Tikkurila, шелковисто-матовая, подготовка Q3	Tikkurila G503 «Calla»	8,2 м²
О5	потолок	окраска, Little Greene Absolute Matt, глубокоматовая, подготовка Q3	Little Greene No. 222 «Loft White»	12,3 м²
О14	плинтус	плинтус МДФ, Orac Decor Contour (Luxxus), h 69 мм, SX165	Tikkurila G503 «Calla»	3,7 м

Изм.	Кол.уч	Лист	№ док.	Подп.	Дата
Разраб.		Кырлан А.С.			04.11.26
Пров.					
ГИП					
Н. контр.					
Утв.					

ГД-2026-012-АИ

Дом 120 м²

Общая площадь 147,36* м² · * размеры приняты, не замерены (реестр — л. 7–9, К-1)

Дизайн-проект интерьера

Стадия	Лист	Листов
РП	150	175

Развёртка стены В. Детская (пом. 7)

М 1:20

Кырлан Александр Сергеевич


выпуск 04.11.2026 № 4dfa962484 · стр. 154 из 180

Развёртка стены Г. Детская (пом. 7)

Детская (пом. 7) · вид изнутри помещения · размеры в мм, отметки в м от ±0,000 (чистый пол 1-го этажа)


ПРЕДВАРИТЕЛЬНО · не для производства работ · открыто пунктов: 11 (реестр — л. 7–9)

Развёртка стены Г

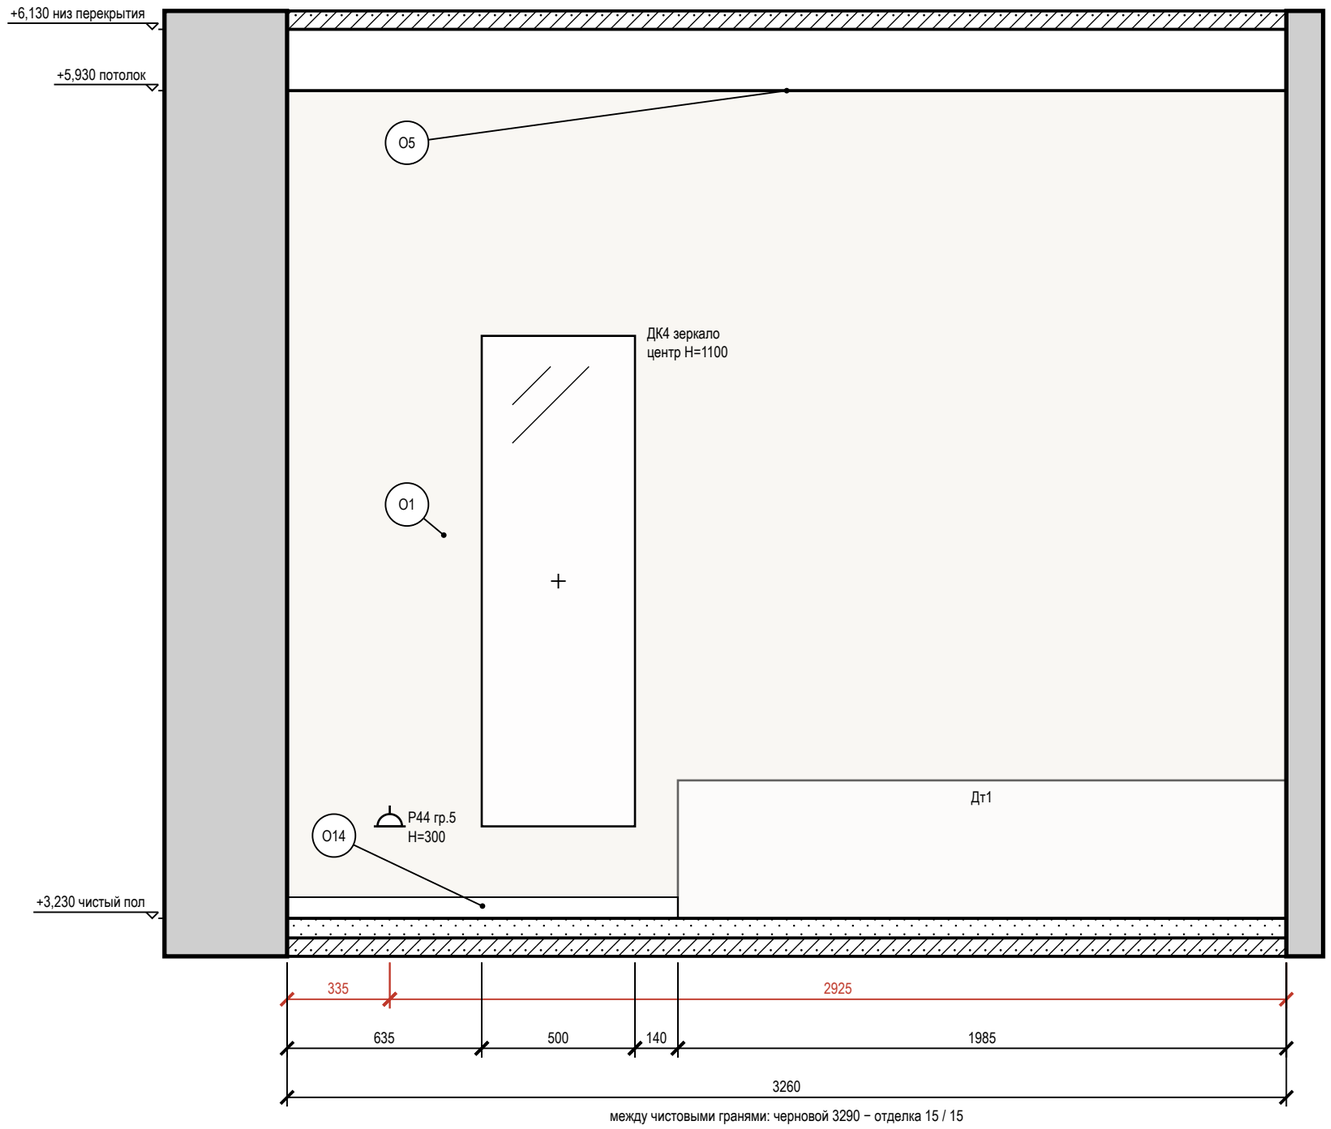

между чистовыми гранями: черновой 3290 − отделка 15 / 15

Схема развёрток (М 1:100)

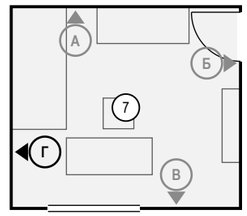

Условные обозначения

- розетка с заземляющим контактом; у знака — марка, ×N постов в рамке, гр. — группа щита, Н — высота оси, мм
- привязки точек и выводов от угла и от пола, мм
- мебель и приборы — фасад по расстановке (условно)
- зеркало: марка Д, крест — центр, Н — высота центра, мм
- стены и перекрытия в сечении
- окраска: тон — цвет по коду производителя (условно)
- О1 — марка отделки по реестру отделки альбома
- А — марка развёртки: буква стены, стрелка — взгляд

Ведомость отделки (на листе)

Марка	Поверхность	Материал, изделие	Цвет, код	Кол.
О1	стены	окраска, Tikkurila, шелковисто-матовая, подготовка Q3	Tikkurila G503 «Calla»	8,8 м²
О5	потолок	окраска, Little Greene Absolute Matt, глубокоматовая, подготовка Q3	Little Greene No. 222 «Loft White»	12,3 м²
О14	плинтус	плинтус МДФ, Orac Decor Contour (Luxxus), h 69 мм, SX165	Tikkurila G503 «Calla»	1,3 м

Допущения и предложения на листе. Основа листа: взаимное расположение помещений, контур дома 9600 × 8000 и раскладка этажей подобраны проектировщиком под габариты помещений брифа; обмер и проект АР — задание (К-1); высота потолка 2900 мм — по брифу, не замерена; перекрытие 330 мм и отметка 2-го этажа +3,230 приняты; проект КР — задание (К-2); наружные стены 400 мм, перегородки 120 мм приняты (в брифе толщин нет) (К-1); разрешённая мощность 15 кВт принята по типовым ТУ для частного дома (К-4); подрайон климата не задан — принят не северный (жилые от 2,5 м) (К-7). Знак «*» — принято, не замерено (замерить): К-1: окно пом. 7 (стена В), дверь пом. 7 (стена Б); К-2: отметка чистого пола этажа «2-й этаж» +3,230. См. лист открытых вопросов (лист 7, записи К-1, К-2, К-4; лист 8, запись К-7).

Примечания

1. Развёртки — вид на стену изнутри помещения, по часовой стрелке; расположение — на схеме листа и на листе 117; размеры — в мм по чистовым поверхностям; отметки — в м от ±0,000 (чистый пол 1-го этажа); высоты Н — от чистого пола помещения до оси изделия, у декора — до центра.
2. Красная цепочка — привязки электроточек и выводов по осям от угла чистовых стен; высота Н — у знака, от чистого пола до оси; высоты мебели, проёмов и границ отделки — колонкой отметок слева. Стена с 5 и более точками или с мелкими звеньями привязок показана двумя видами: архитектурная развёртка (мебель, отделка, проёмы, высоты) и вид «Привязки» на отдельном листе — точки и выводы с марками, одна цепочка по осям и таблица привязок (каждая точка — строка).
3. У знака электроточки: марка (Р — розетка, S — выключатель, Св — светильник, ЭВ — вывод кабеля), ×N — число постов в рамке, гр. — группа щита, Н — высота оси от чистого пола, мм; группы по клавишам выключателя — на листе выключателей.
4. Схема мебели, приборов и декора не является технической документацией для производства мебели; габариты — по паспортам изделий.
5. Картины и зеркала крепить к основанию по паспорту изделия (закладные и анкеры — в перечне скрытых работ); крест — ось центра предмета.
6. Потолок — у каждой стены свой, по плану потолков (ПТ8); ступени — зоной, кромка короба перед нишей — тонкой линией; в поле потолка: ПТ7 +6,030.

1000 мм · печать 1:1

Изм.	Кол.уч	Лист	№ док.	Подп.	Дата
Разраб.		Кырлан А.С.			04.11.26
Пров.					
ГИП					
Н. контр.					
Утв.					

ГД-2026-012-АИ

Дом 120 м²

Общая площадь 147,36* м² · * размеры приняты, не замерены (реестр — л. 7–9, К-1)

Дизайн-проект интерьера

Стадия	Лист	Листов
РП	151	175

Развёртка стены Г. Детская (пом. 7)

М 1:20

Кырлан Александр Сергеевич


выпуск 04.11.2026 № 4dfa962484 · стр. 155 из 180

Развёртки стен А, Б. Гардеробная (пом. 8)

Гардеробная (пом. 8) · вид изнутри помещения · размеры в мм, отметки в м от ±0,000 (чистый пол 1-го этажа)


ПРЕДВАРИТЕЛЬНО · не для производства работ · открыто пунктов: 11 (реестр — л. 7–9)

Развёртка стены А

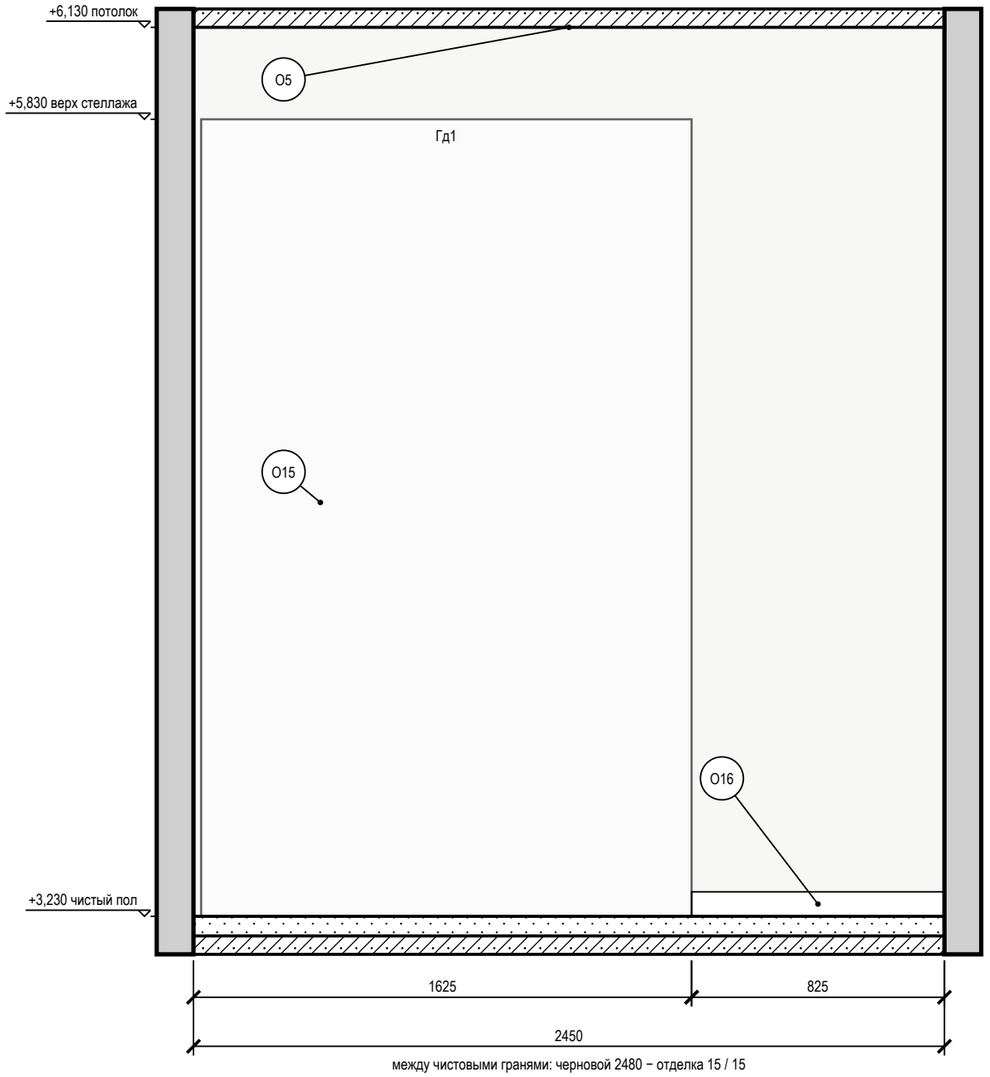


между чистовыми гранями: черновой 2480 − отделка 15 / 15

Развёртка стены Б

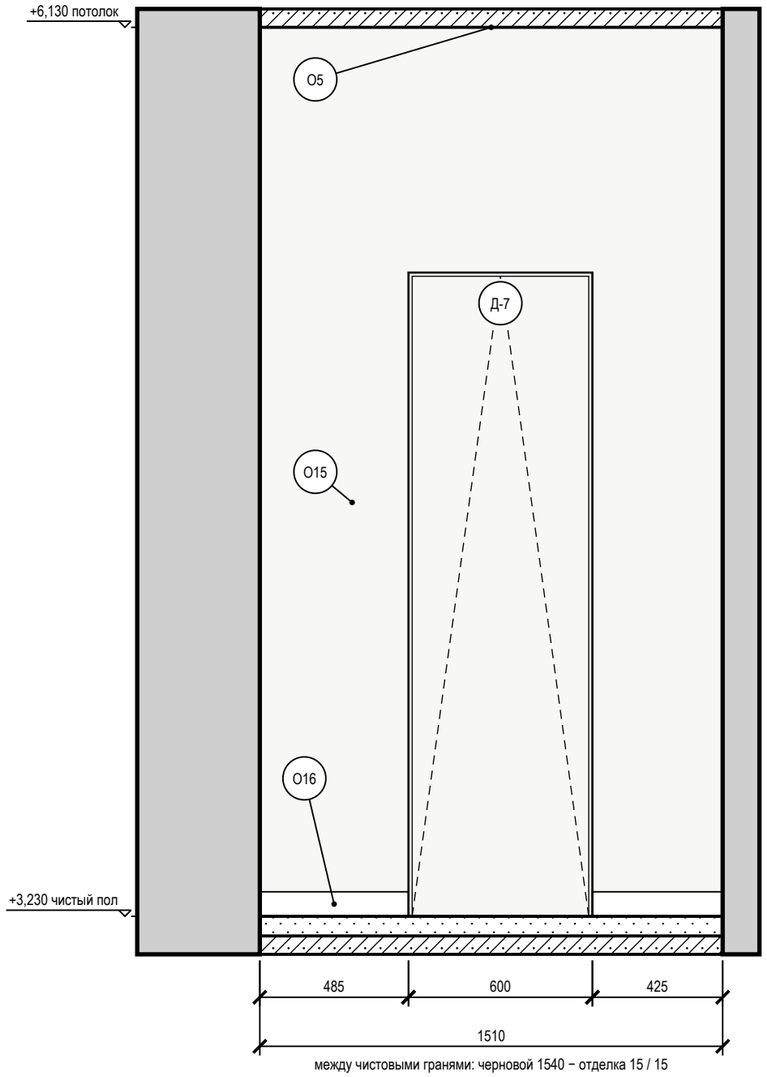

между чистовыми гранями: черновой 1540 − отделка 15 / 15

Схема развёрток (М 1:100)

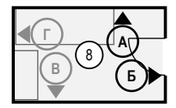

Условные обозначения

- мебель и приборы — фасад по расстановке (условно)
- дверь скрытого монтажа: полотно в плоскости стены (узел — на листе узлов)
- стены и перекрытия в сечении
- окраска: тон — цвет по коду производителя (условно)
- О1 — марка отделки по реестру отделки альбома
- А — марка развёртки: буква стены, стрелка — взгляд

Допущения и предложения на листе

Основа листа: взаимное расположение помещений, контур дома 9600 × 8000 и раскладка этажей подобраны проектировщиком под габариты помещений брифа; обмер и проект АР — задание (К-1); высота потолка 2900 мм — по брифу, не замерена; перекрытие 330 мм и отметка 2-го этажа +3,230 приняты; проект КР — задание (К-2); наружные стены 400 мм, перегородки 120 мм приняты (в брифе толщин нет) (К-1); разрешённая мощность 15 кВт принята по типовым ТУ для частного дома (К-4); подрайон климата не задан — принят не северный (жилые от 2,5 м) (К-7).

Знак «*» — принято, не замерено и не подтверждено (замерить на объекте): К-1: дверь пом. 8 (стена Б) — проём: место и ширина приняты проектировщиком по брифу (раскладка этажей — К-1), не замерены; К-2: отметка чистого пола этажа «2-й этаж» +3,230 — отметка чистого пола 2-го этажа +3,230 принята: высота потолка 2900 по брифу + перекрытие с полом 330 (конструкция перекрытия не задана; проект КР — задание).

См. лист открытых вопросов (лист 7, записи К-1, К-2, К-4; лист 8, запись К-7).

Примечания

1. Развёртки — вид на стену изнутри помещения, по часовой стрелке; расположение — на схеме листа и на листе 117; размеры — в мм по чистовым поверхностям; отметки — в м от ±0,000 (чистый пол 1-го этажа); высоты Н — от чистого пола помещения до оси изделия, у декора — до центра.
2. Схема мебели, приборов и декора не является технической документацией для производства мебели; габариты — по паспортам изделий.
3. Двери скрытого монтажа — полотно в плоскости стены, отделка стены по полотну, плинтус прерывается у короба (узел — на листе узлов).

1000 мм · печать 1:1

Изм.	Кол.уч	Лист	№ док.	Подп.	Дата
Разраб.		Кырлан А.С.			04.11.26
Пров.					
ГИП					
Н. контр.					
Утв.					

ГД-2026-012-АИ

Дом 120 м²

Общая площадь 147,36* м² · * размеры приняты, не замерены (реестр — л. 7–9, К-1)

Дизайн-проект интерьера

Стадия	Лист	Листов
РП	152	175

Развёртки стен А, Б. Гардеробная (пом. 8)

М 1:20

Кырлан Александр Сергеевич


выпуск 04.11.2026 № 4dfa962484 · стр. 156 из 180

Развёртки стен В, Г. Гардеробная (пом. 8)

Гардеробная (пом. 8) · вид изнутри помещения · размеры в мм, отметки в м от ±0,000 (чистый пол 1-го этажа)


ПРЕДВАРИТЕЛЬНО · не для производства работ · открыто пунктов: 11 (реестр — л. 7–9)

Развёртка стены В

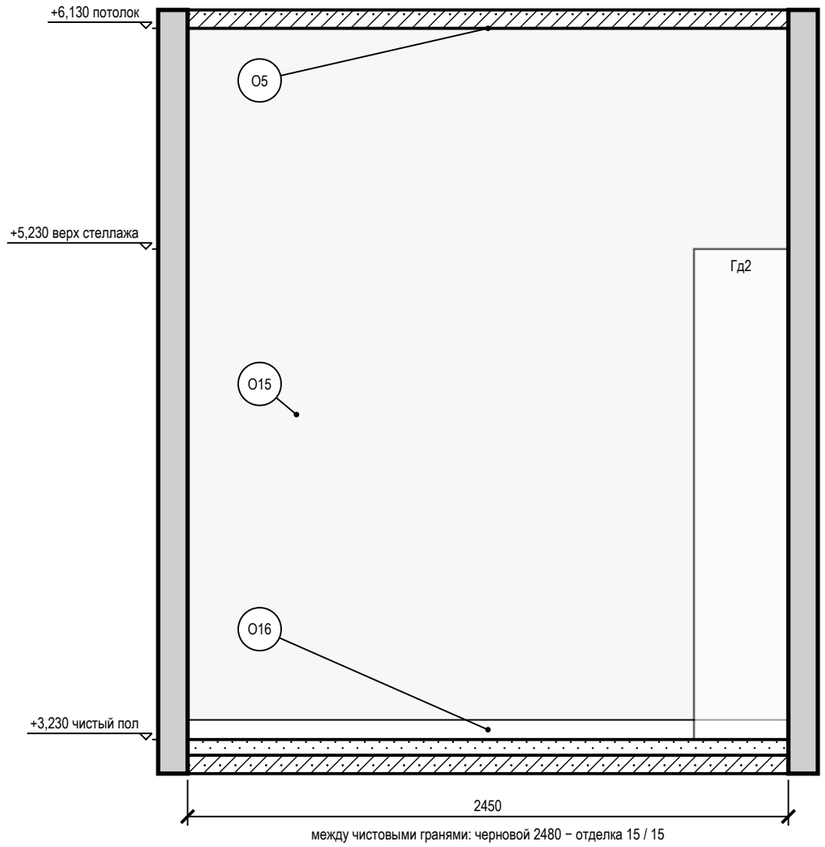


между чистовыми гранями: черновой 2480 − отделка 15 / 15

Развёртка стены Г

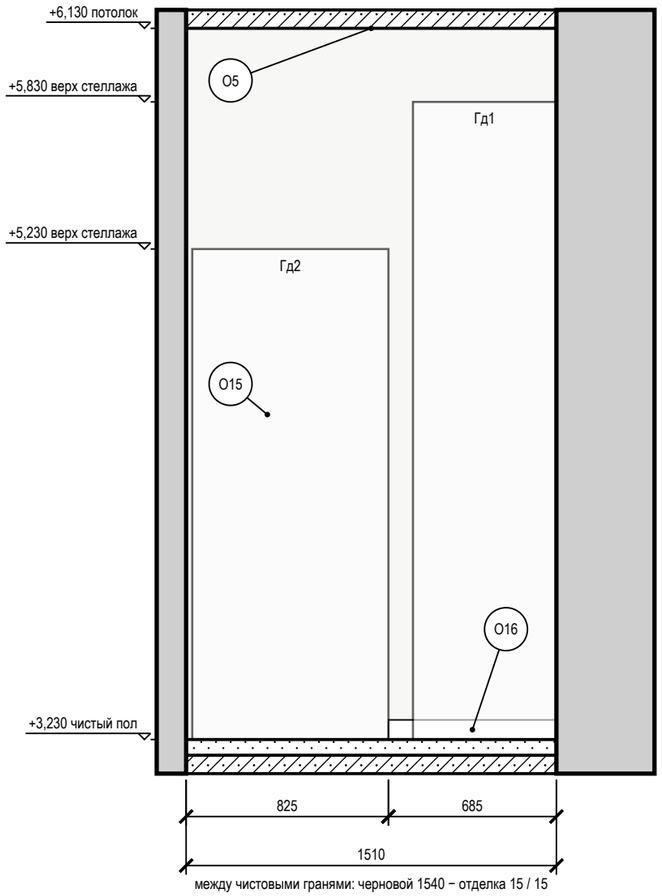

между чистовыми гранями: черновой 1540 − отделка 15 / 15

Схема развёрток (М 1:100)

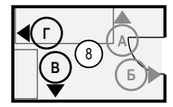

Условные обозначения

- мебель и приборы — фасад по расстановке (условно)
- стены и перекрытия в сечении
- окраска: тон — цвет по коду производителя (условно)
- О1 — марка отделки по реестру отделки альбома
- А — марка развёртки: буква стены, стрелка — взгляд

Ведомость отделки (на листе)

Марка	Поверхность	Материал, изделие	Цвет, код	Кол.
О5	потолок	окраска, Little Greene Absolute Matt, глубокоматовая, подготовка Q3	Little Greene No. 222 «Loft White»	3,8 м²
О15	стены	окраска, Little Greene Intelligent Matt, матовая, подготовка Q3	Little Greene No. 222 «Loft White»	11,5 м²
О16	плинтус	плинтус МДФ, h 80 мм, аналог: плинтус МДФ под покраску 80×16	Little Greene No. 222 «Loft White»	3,1 м

Допущения и предложения на листе

Основа листа: взаимное расположение помещений, контур дома 9600 × 8000 и раскладка этажей подобраны проектировщиком под габариты помещений брифа; обмер и проект АР — задание (К-1); высота потолка 2900 мм — по брифу, не замерена; перекрытие 330 мм и отметка 2-го этажа +3,230 приняты; проект КР — задание (К-2); наружные стены 400 мм, перегородки 120 мм приняты (в брифе толщин нет) (К-1); разрешённая мощность 15 кВт принята по типовым ТУ для частного дома (К-4); подрайон климата не задан — принят не северный (жилые от 2,5 м) (К-7).

Знак «*» — принято, не замерено и не подтверждено (замерить на объекте): К-1: дверь пом. 8 (стена Б) — проём: место и ширина приняты проектировщиком по брифу (раскладка этажей — К-1), не замерены; К-2: отметка чистого пола этажа «2-й этаж» +3,230 — отметка чистого пола 2-го этажа +3,230 принята: высота потолка 2900 по брифу + перекрытие с полом 330 (конструкция перекрытия не задана; проект КР — задание).

См. лист открытых вопросов (лист 7, записи К-1, К-2, К-4; лист 8, запись К-7).

Примечания

1. Развёртки — вид на стену изнутри помещения, по часовой стрелке; расположение — на схеме листа и на листе 117; размеры — в мм по чистовым поверхностям; отметки — в м от ±0,000 (чистый пол 1-го этажа); высоты Н — от чистого пола помещения до оси изделия, у декора — до центра.
2. Схема мебели, приборов и декора не является технической документацией для производства мебели; габариты — по паспортам изделий.

1000 мм · печать 1:1

Изм.	Кол.уч	Лист	№ док.	Подп.	Дата
Разраб.		Кырлан А.С.			04.11.26
Пров.					
ГИП					
Н. контр.					
Утв.					

ГД-2026-012-АИ

Дом 120 м²

Общая площадь 147,36* м² · * размеры приняты, не замерены (реестр — л. 7–9, К-1)

Дизайн-проект интерьера

Стадия	Лист	Листов
РП	153	175

Развёртки стен В, Г. Гардеробная (пом. 8)

М 1:25

Кырлан Александр Сергеевич


выпуск 04.11.2026 № 4dfa962484 · стр. 157 из 180

Развёртки стен. Кладовая (пом. 9)

Кладовая (пом. 9) · вид изнутри помещения · размеры в мм, отметки в м от ±0,000 (чистый пол 1-го этажа)


ПРЕДВАРИТЕЛЬНО · не для производства работ · открыто пунктов: 11 (реестр — л. 7–9)

Развёртка стены Б

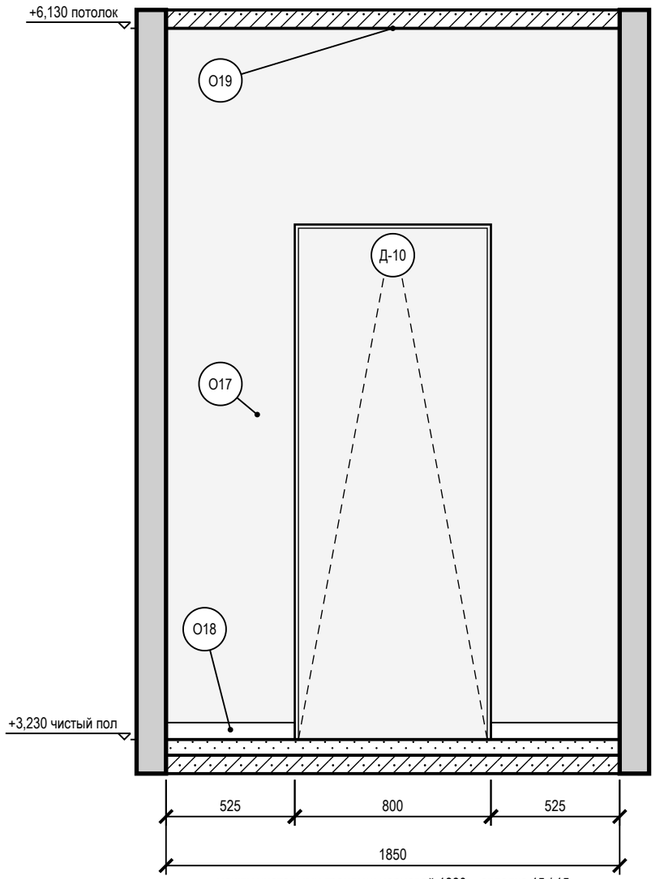


между чистовыми гранями: черновой 1880 − отделка 15 / 15

Развёртка стены В

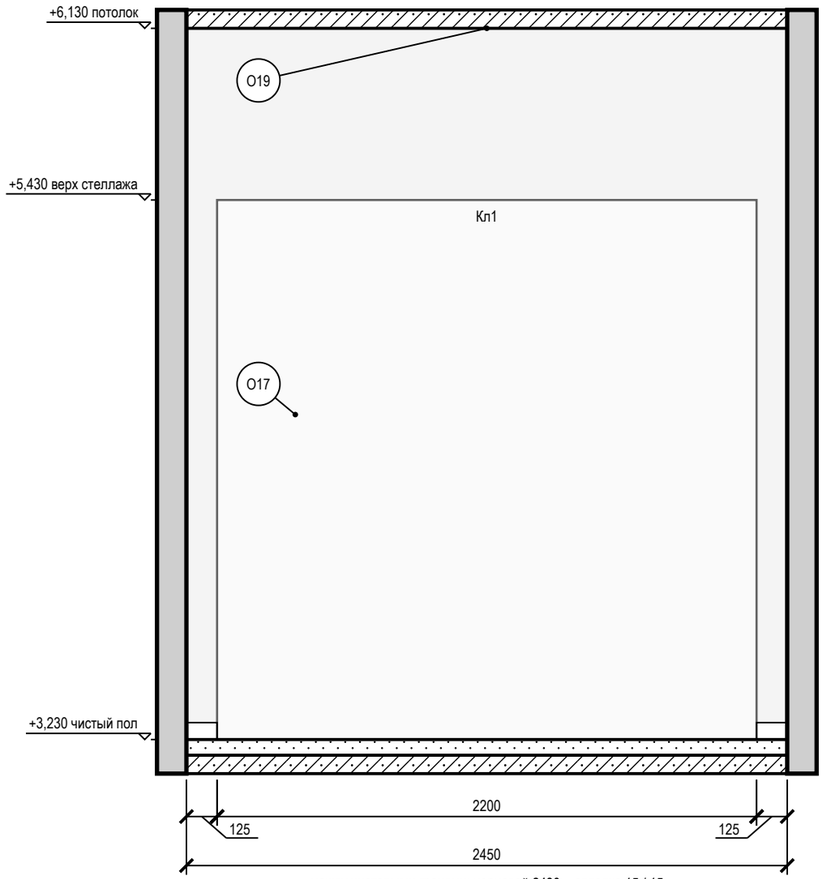


между чистовыми гранями: черновой 2480 − отделка 15 / 15

Развёртка стены Г

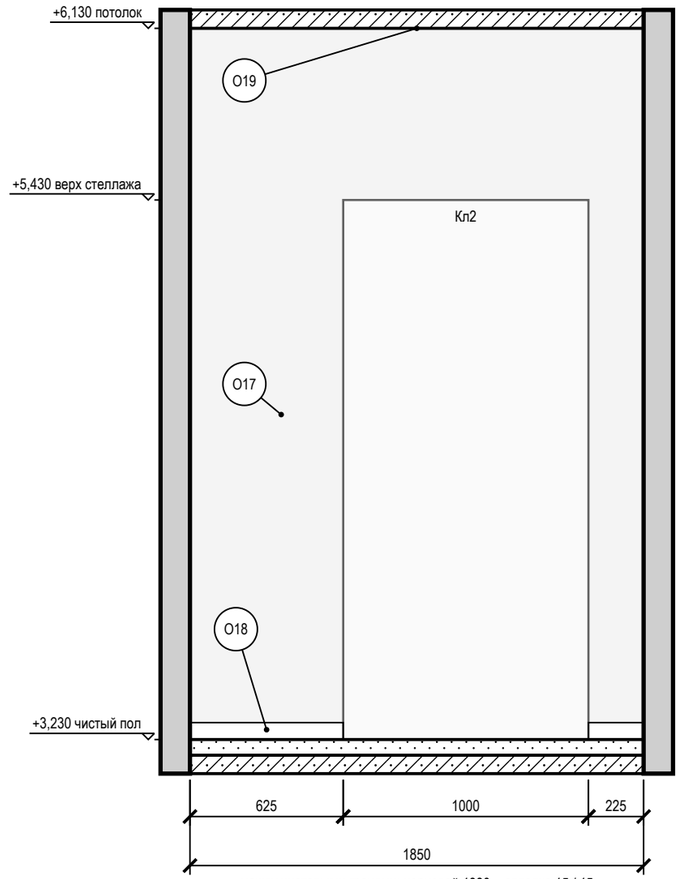

между чистовыми гранями: черновой 1880 − отделка 15 / 15

Схема развёрток (М 1:100)

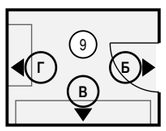

Условные обозначения

- мебель и приборы — фасад по расстановке (условно)
- дверь скрытого монтажа: полотно в плоскости стены (узел — на листе узлов)
- стены и перекрытия в сечении
- О1 — марка отделки по реестру отделки альбома
- А — марка развёртки: буква стены, стрелка — взгляд

Ведомость отделки (на листе)

Марка	Поверхность	Материал, изделие	Цвет, код	Кол.
О17	стены	окраска, Tikkurila, матовая, подготовка Q3	NCS S 0502-Y	16,2 м²
О18	плинтус	плинтус МДФ, Orac Decor Contour (Luxxus), h 69 мм, SX165, шелковисто-матовая	NCS S 0300-N	2,1 м
О19	потолок	окраска, Tikkurila, глубокоматовая	NCS S 0300-N	4,7 м²

Примечания

1. Развёртки — вид на стену изнутри помещения, по часовой стрелке; расположение — на схеме листа и на листе 117; размеры — в мм по чистовым поверхностям; отметки — в м от ±0,000 (чистый пол 1-го этажа); высоты Н — от чистого пола помещения до оси изделия, у декора — до центра.
2. Схема мебели, приборов и декора не является технической документацией для производства мебели; габариты — по паспортам изделий.
3. Двери скрытого монтажа — полотно в плоскости стены, отделка стены по полотну, плинтус прерывается у короба (узел — на листе узлов).

Допущения и предложения на листе. Основа листа: взаимное расположение помещений, контур дома 9600 × 8000 и раскладка этажей подобраны проектировщиком под габариты помещений брифа; обмер и проект АР — задание (К-1); высота потолка 2900 мм — по брифу, не замерена; перекрытие 330 мм и отметка 2-го этажа +3,230 приняты; проект КР — задание (К-2); наружные стены 400 мм, перегородки 120 мм приняты (в брифе толщин нет) (К-1); разрешённая мощность 15 кВт принята по типовым ТУ для частного дома (К-4); подрайон климата не задан — принят не северный (жилые от 2,5 м) (К-7). Знак «*» — принято, не замерено и не подтверждено (замерить на объекте): К-1: дверь пом. 9 (стена Б) — проём: место и ширина приняты проектировщиком по брифу (раскладка этажей — К-1), не замерены; К-2: отметка чистого пола этажа «2-й этаж» +3,230 — отметка чистого пола 2-го этажа +3,230 принята: высота потолка 2900 по брифу + перекрытие с полом 330 (конструкция перекрытия не задана; проект КР — задание). См. лист открытых вопросов (лист 7, записи К-1, К-2, К-4; лист 8, запись К-7).

1000 мм · печать 1:1

Изм.	Кол.уч	Лист	№ док.	Подп.	Дата
Разраб.		Кырлан А.С.			04.11.26
Пров.					
ГИП					
Н. контр.					
Утв.					

ГД-2026-012-АИ

Дом 120 м²

Общая площадь 147,36* м² · * размеры приняты, не замерены (реестр — л. 7–9, К-1)

Дизайн-проект интерьера

Стадия	Лист	Листов
РП	154	175

Развёртки стен. Кладовая (пом. 9)

М 1:25

Кырлан Александр Сергеевич


выпуск 04.11.2026 № 4dfa962484 · стр. 158 из 180

Развёртка стены А. Холл второго этажа (пом. 10)

Холл второго этажа (пом. 10) · вид изнутри помещения · размеры в мм, отметки в м от ±0,000 (чистый пол 1-го этажа)


ПРЕДВАРИТЕЛЬНО · не для производства работ · открыто пунктов: 11 (реестр — л. 7–9)

Развёртка стены А

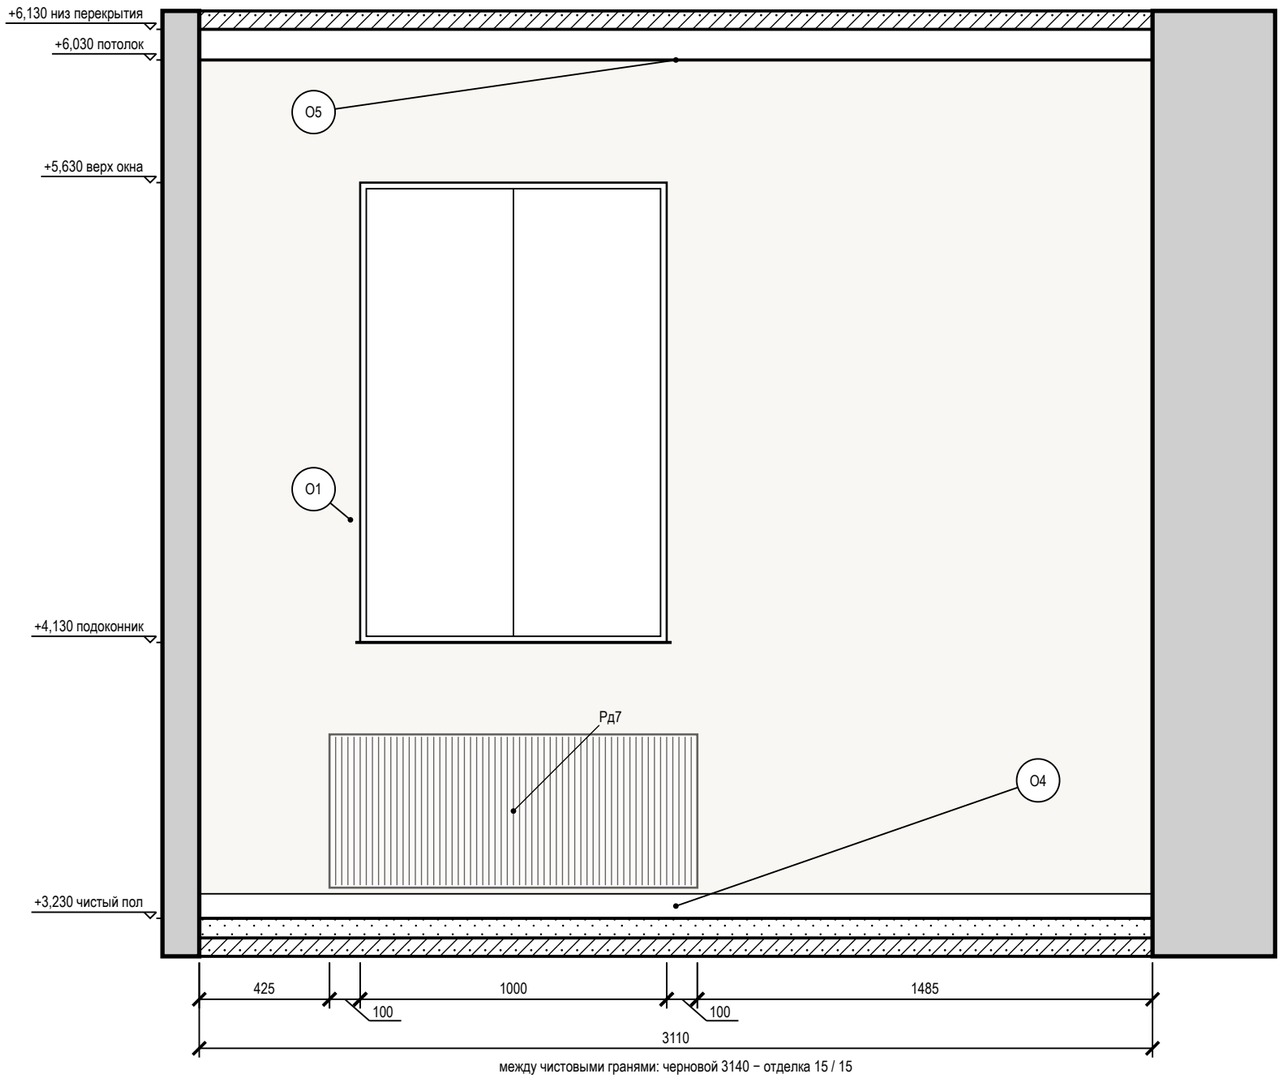

между чистовыми гранями: черновой 3140 − отделка 15 / 15

Схема развёрток (М 1:100)

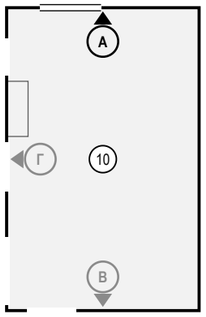

Условные обозначения

- мебель и приборы — фасад по расстановке (условно)
- окно: проём, рама, подоконник
- радиатор отопления; марка — по плану отопления
- стены и перекрытия в сечении
- окраска: тон — цвет по коду производителя (условно)
- О1 — марка отделки по реестру отделки альбома
- А — марка развёртки: буква стены, стрелка — взгляд

Ведомость отделки (на листе)

Марка	Поверхность	Материал, изделие	Цвет, код	Кол.
О1	стены	окраска, Tikkurila, матовая, подготовка Q3	Tikkurila G503 «Calla»	7,2 м²
О4	плинтус	плинтус МДФ, h 80 мм, аналог: плинтус МДФ под покраску 80×16	Tikkurila G503 «Calla»	3,1 м
О5	потолок	окраска, Little Greene Absolute Matt, глубокоматовая, подготовка Q3	Little Greene No. 222 «Loft White»	15,5 м²

Примечания

1. Развёртки — вид на стену изнутри помещения, по часовой стрелке; расположение — на схеме листа и на листе 117; размеры — в мм по чистовым поверхностям; отметки — в м от ±0,000 (чистый пол 1-го этажа); высоты Н — от чистого пола помещения до оси изделия, у декора — до центра.
2. Схема мебели, приборов и декора не является технической документацией для производства мебели; габариты — по паспортам изделий.

Допущения и предложения на листе. Основа листа: взаимное расположение помещений, контур дома 9600 × 8000 и раскладка этажей подобраны проектировщиком под габариты помещений брифа; обмер и проект АР — задание (К-1); высота потолка 2900 мм — по брифу, не замерена; перекрытие 330 мм и отметка 2-го этажа +3,230 приняты; проект КР — задание (К-2); наружные стены 400 мм, перегородки 120 мм приняты (в брифе толщин нет) (К-1); разрешённая мощность 15 кВт принята по типовым ТУ для частного дома (К-4); подрайон климата не задан — принят не северный (жилые от 2,5 м) (К-7). Знак «*» — принято, не замерено и не подтверждено (замерить на объекте): К-1: окно пом. 10 (стена А) — окно: место, ширина, высота и подоконник приняты по брифу, стена — по раскладке проектировщика (К-1), не замерены; К-2: отметка чистого пола этажа «2-й этаж» +3,230 — отметка чистого пола 2-го этажа +3,230 принята: высота потолка 2900 по брифу + перекрытие с полом 330 (конструкция перекрытия не задана; проект КР — задание). См. лист открытых вопросов (лист 7, записи К-1, К-2, К-4; лист 8, запись К-7; лист 9, запись ИЗ-2); по листу — ИЗ-2.

1000 мм · печать 1:1

Изм.	Кол.уч	Лист	№ док.	Подп.	Дата
Разраб.		Кырлан А.С.			04.11.26
Пров.					
ГИП					
Н. контр.					
Утв.					

ГД-2026-012-АИ

Дом 120 м²

Общая площадь 147,36* м² · * размеры приняты, не замерены (реестр — л. 7–9, К-1)

Дизайн-проект интерьера

Стадия	Лист	Листов
РП	155	175

Развёртка стены А. Холл второго этажа (пом. 10)

М 1:20

Кырлан Александр Сергеевич

выпуск 04.11.2026 № 4dfa962484 · стр. 159 из 180

Развёртка стены В. Холл второго этажа (пом. 10)

Холл второго этажа (пом. 10) · вид изнутри помещения · размеры в мм, отметки в м от ±0,000 (чистый пол 1-го этажа)

ПРЕДВАРИТЕЛЬНО · не для производства работ · открыто пунктов: 11 (реестр — л. 7–9)

Развёртка стены В


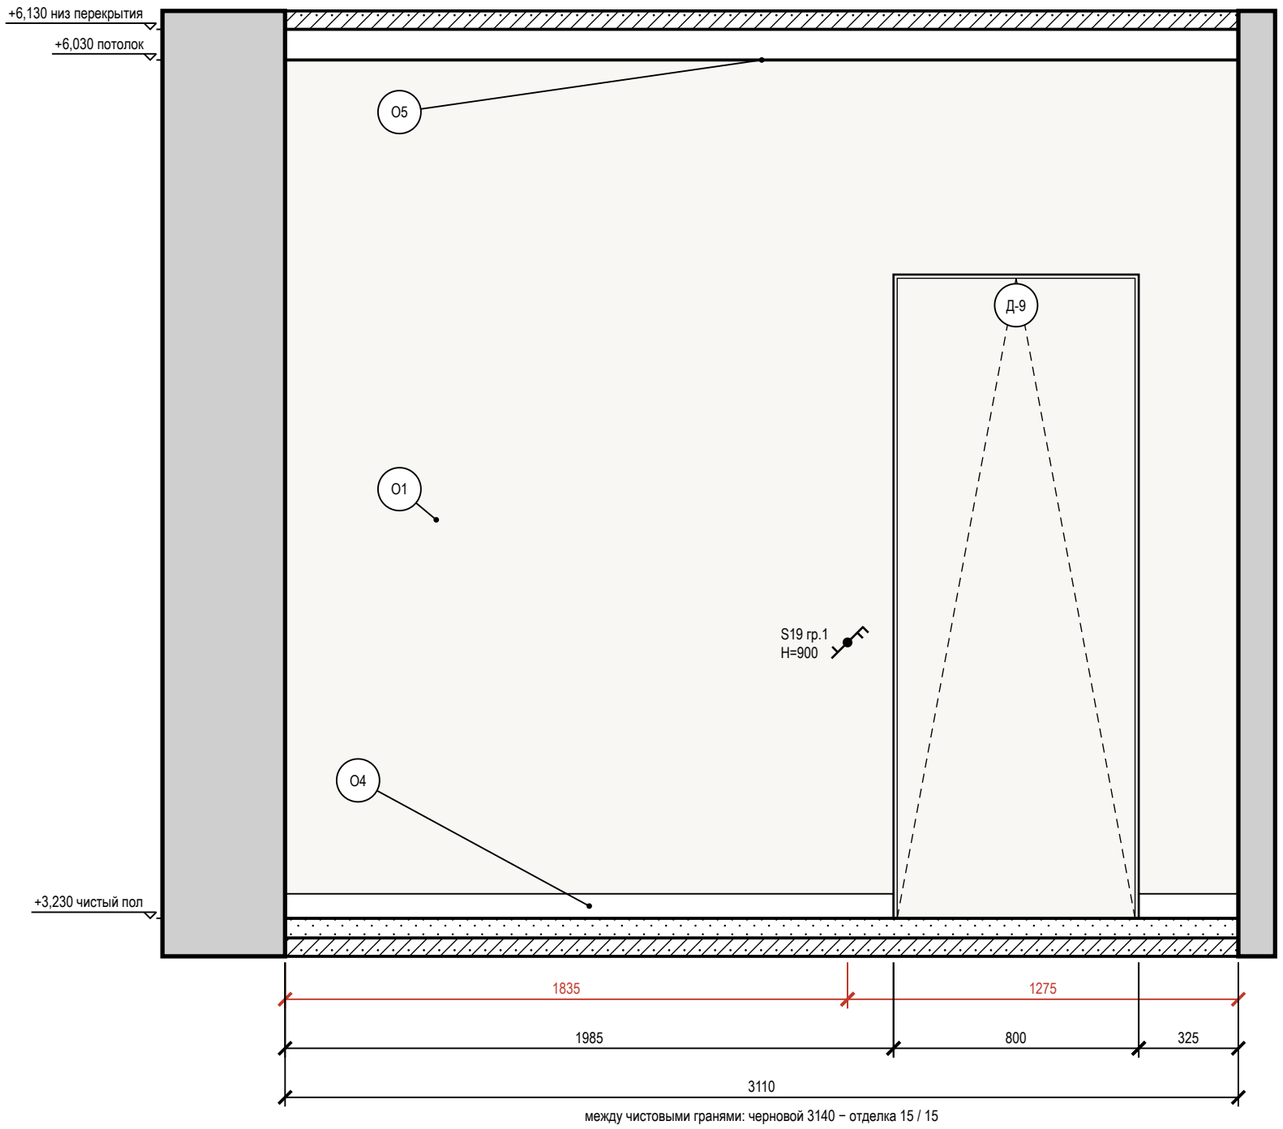


Схема развёрток (М 1:100)

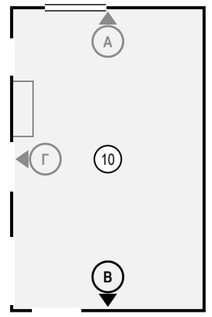

Допущения и предложения на листе. Основа листа: взаимное расположение помещений, контур дома 9600 × 8000 и раскладка этажей подобраны проектировщиком под габариты помещений брифа; обмер и проект АР — задание (К-1); высота потолка 2900 мм — по брифу, не замерена; перекрытие 330 мм и отметка 2-го этажа +3,230 приняты; проект КР — задание (К-2); наружные стены 400 мм, перегородки 120 мм приняты (в брифе толщин нет) (К-1); разрешённая мощность 15 кВт принята по типовым ТУ для частного дома (К-4); подрайон климата не задан — принят не северный (жилые от 2,5 м) (К-7). Знак «*» — принято, не замерено и не подтверждено (замерить на объекте): К-1: окно пом. 10 (стена А) — окно: место, ширина, высота и подоконник приняты по брифу, стена — по раскладке проектировщика (К-1), не замерены; К-2: отметка чистого пола этажа «2-й этаж» +3,230 — отметка чистого пола 2-го этажа +3,230 принята: высота потолка 2900 по брифу + перекрытие с полом 330 (конструкция перекрытия не задана; проект КР — задание). См. лист открытых вопросов (лист 7, записи К-1, К-2, К-4; лист 8, запись К-7).

Условные обозначения

- выключатель одноклавишный
- выключатель двухклавишный (флажков — по числу клавиш)
- выключатель с проходной или перекрёстной клавишей (обратный флажок); тип клавиши — в подписи
- привязки точек и выводов от угла и от пола, мм
- мебель и приборы — фасад по расстановке (условно)
- дверь скрытого монтажа: полотно в плоскости стены (узел — на листе узлов)
- стены и перекрытия в сечении
- окраска: тон — цвет по коду производителя (условно)
- О1 — марка отделки по реестру отделки альбома
- А — марка развёртки: буква стены, стрелка — взгляд

Ведомость отделки (на листе)

Марка	Поверхность	Материал, изделие	Цвет, код	Кол.
О1	стены	окраска, Tikkurila, матовая, подготовка Q3	Tikkurila G503 «Calla»	7 м²
О4	плинтус	плинтус МДФ, h 80 мм, аналог: плинтус МДФ под покраску 80×16	Tikkurila G503 «Calla»	2,3 м
О5	потолок	окраска, Little Greene Absolute Matt, глубокоматовая, подготовка Q3	Little Greene No. 222 «Loft White»	15,5 м²

Примечания

1. Развёртки — вид на стену изнутри помещения, по часовой стрелке; расположение — на схеме листа и на листе 117; размеры — в мм по чистовым поверхностям; отметки — в м от ±0,000 (чистый пол 1-го этажа); высоты Н — от чистого пола помещения до оси изделия, у декора — до центра.
2. Красная цепочка — привязки электроточек и выводов по осям от угла чистовых стен; высота Н — у знака, от чистого пола до оси; высоты мебели, проёмов и границ отделки — колонкой отметок слева. Стена с 5 и более точками или с мелкими звеньями привязок показана двумя видами: архитектурная развёртка (мебель, отделка, проёмы, высоты) и вид «Привязки» на отдельном листе — точки и выводы с марками, одна цепочка по осям и таблица привязок (каждая точка — строка).
3. У знака электроточки: марка (Р — розетка, S — выключатель, Св — светильник, ЭВ — вывод кабеля), ×N — число постов в рамке, гр. — группа щита, Н — высота оси от чистого пола, мм; группы по клавишам выключателя — на листе выключателей.
4. Схема мебели, приборов и декора не является технической документацией для производства мебели; габариты — по паспортам изделий.
5. Двери скрытого монтажа — полотно в плоскости стены, отделка стены по полотну, плинтус прерывается у короба (узел — на листе узлов).

1000 мм · печать 1:1

Изм.	Кол.уч	Лист	№ док.	Подп.	Дата
Разраб.		Кырлан А.С.			04.11.26
Пров.					
ГИП					
Н. контр.					
Утв.					

ГД-2026-012-АИ

Дом 120 м²

Общая площадь 147,36* м² · * размеры приняты, не замерены (реестр — л. 7–9, К-1)

Дизайн-проект интерьера	Стадия	Лист	Листов
	РП	156	175

Развёртка стены В. Холл второго этажа (пом. 10)

М 1:20

Кырлан Александр Сергеевич


выпуск 04.11.2026 № 4dfa962484 · стр. 160 из 180

Развёртка стены Г. Холл второго этажа (пом. 10)

Холл второго этажа (пом. 10) · вид изнутри помещения · размеры в мм, отметки в м от ±0,000 (чистый пол 1-го этажа)


ПРЕДВАРИТЕЛЬНО · не для производства работ · открыто пунктов: 11 (реестр — л. 7–9)

Развёртка стены Г

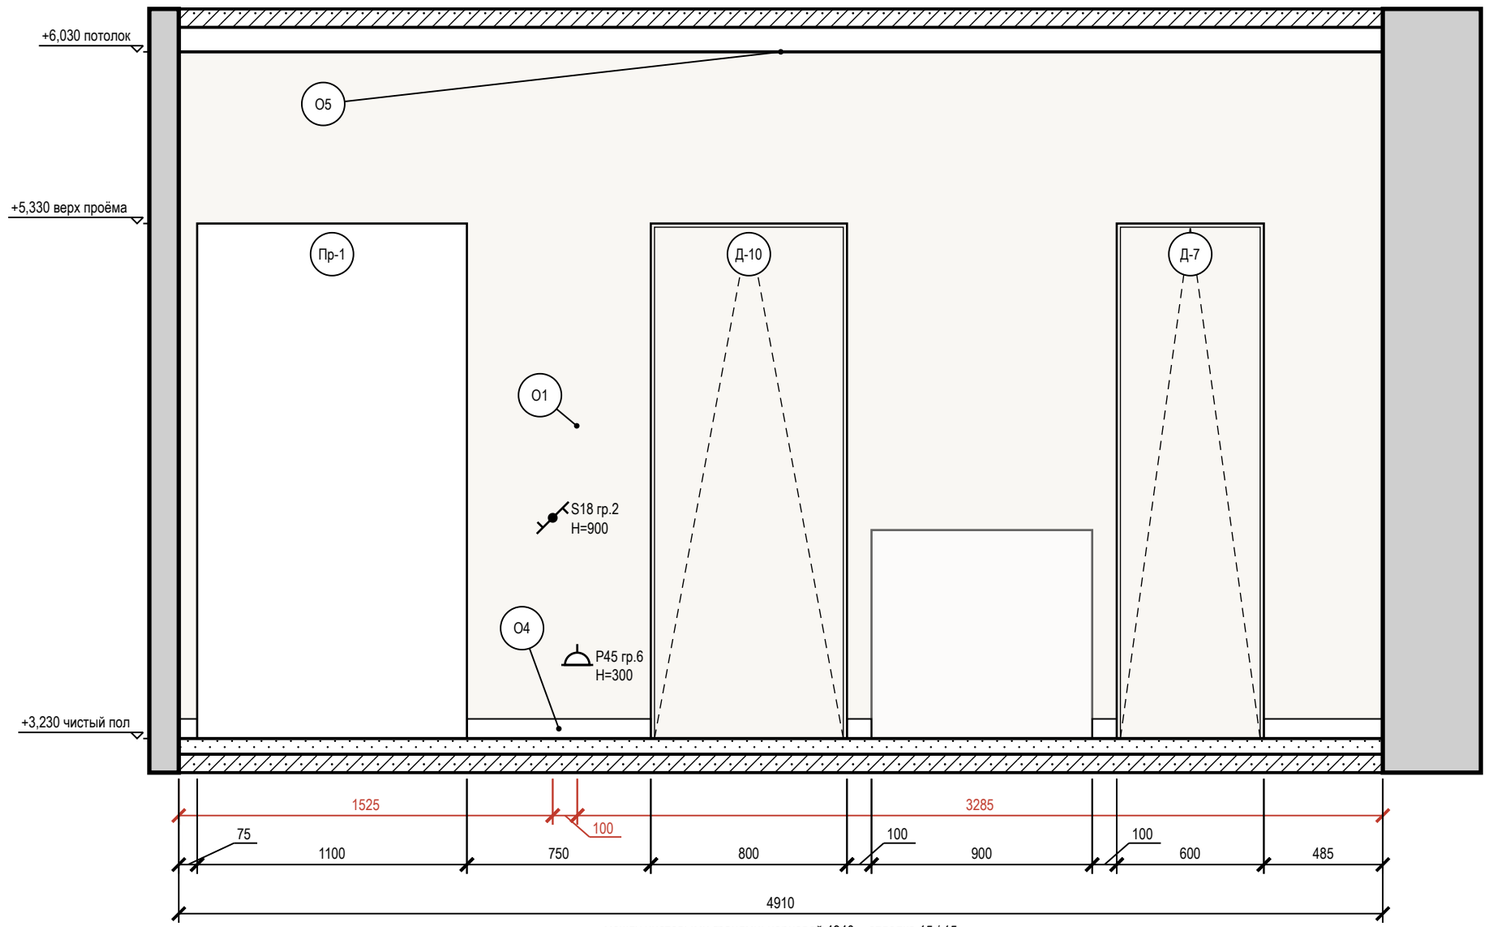

между чистовыми гранями: черновой 4940 − отделка 15 / 15

Схема развёрток (М 1:100)

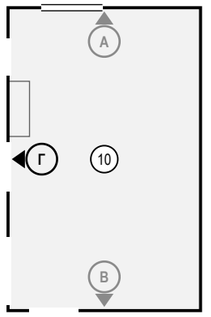

Условные обозначения

- розетка с заземляющим контактом; у знака — марка, ×N постов в рамке, гр. — группа щита, H — высота оси, мм
- выключатель одноклавишный
- выключатель с проходной или перекрёстной клавишей (обратный флажок); тип клавиши — в подписи
- привязки точек и выводов от угла и от пола, мм
- мебель и приборы — фасад по расстановке (условно)
- дверь скрытого монтажа: полотно в плоскости стены (узел — на листе узлов)
- дверной проём; марка двери — в кружке
- стены и перекрытия в сечении
- окраска: тон — цвет по коду производителя (условно)
- О1 — марка отделки по реестру отделки альбома
- А — марка развёртки: буква стены, стрелка — взгляд

Ведомость отделки (на листе)

Марка	Поверхность	Материал, изделие	Цвет, код	Кол.
О1	стены	окраска, Tikkurila, матовая, подготовка Q3	Tikkurila G503 «Calla»	8,5 м²
О4	плинтус	плинтус МДФ, h 80 мм, аналог: плинтус МДФ под покраску 80×16	Tikkurila G503 «Calla»	1,5 м
О5	потолок	окраска, Little Greene Absolute Matt, глубокоматовая, подготовка Q3	Little Greene No. 222 «Loft White»	15,5 м²

Допущения и предложения на листе

Основа листа: взаимное расположение помещений, контур дома 9600 × 8000 и раскладка этажей подобраны проектировщиком под габариты помещений брифа; обмер и проект АР — задание (К-1); высота потолка 2900 мм — по брифу, не замерена; перекрытие 330 мм и отметка 2-го этажа +3,230 приняты; проект КР — задание (К-2); наружные стены 400 мм, перегородки 120 мм приняты (в брифе толщин нет) (К-1); разрешённая мощность 15 кВт принята по типовым ТУ для частного дома (К-4); подрайон климата не задан — принят не северный (жилые от 2,5 м) (К-7).
Знак «*» — принято, не замерено и не подтверждено (замерить на объекте): К-1: окно пом. 10 (стена А) — окно: место, ширина, высота и подоконник приняты по брифу, стена — по раскладке проектировщика (К-1), не замерены; К-2: отметка чистого пола этажа «2-й этаж» +3,230 — отметка чистого пола 2-го этажа +3,230 принята: высота потолка 2900 по брифу + перекрытие с полом 330 (конструкция перекрытия не задана; проект КР — задание).
См. лист открытых вопросов (лист 7, записи К-1, К-2, К-4; лист 8, запись К-7).

Примечания

1. Развёртки — вид на стену изнутри помещения, по часовой стрелке; расположение — на схеме листа и на листе 117; размеры — в мм по чистовым поверхностям; отметки — в м от ±0,000 (чистый пол 1-го этажа); высоты H — от чистого пола помещения до оси изделия, у декора — до центра.
2. Красная цепочка — привязки электроточек и выводов по осям от угла чистовых стен; высота H — у знака, от чистого пола до оси; высоты мебели, проёмов и границ отделки — колонкой отметок слева. Стена с 5 и более точками или с мелкими звеньями привязок показана двумя видами: архитектурная развёртка (мебель, отделка, проёмы, высоты) и вид «Привязки» на отдельном листе — точки и выводы с марками, одна цепочка по осям и таблица привязок (каждая точка — строка).
3. У знака электроточки: марка (Р — розетка, S — выключатель, Св — светильник, ЭВ — вывод кабеля), ×N — число постов в рамке, гр. — группа щита, H — высота оси от чистого пола, мм; группы по клавишам выключателя — на листе выключателей.
4. Схема мебели, приборов и декора не является технической документацией для производства мебели; габариты — по паспортам изделий.
5. Двери скрытого монтажа — полотно в плоскости стены, отделка стены по полотну, плинтус прерывается у короба (узел — на листе узлов).

1000 мм · печать 1:1

Изм.	Кол.уч	Лист	№ док.	Подп.	Дата
Разраб.		Кырлан А.С.			04.11.26
Пров.					
ГИП					
Н. контр.					
Утв.					

ГД-2026-012-АИ

Дом 120 м²

Общая площадь 147,36* м² · * размеры приняты, не замерены (реестр — л. 7–9, К-1)

Дизайн-проект интерьера

Стадия	Лист	Листов
РП	157	175

Развёртка стены Г. Холл второго этажа (пом. 10)

М 1:25

Кырлан Александр Сергеевич


выпуск 04.11.2026 № 4dfa962484 · стр. 161 из 180

Развёртки стен А, В. Коридор второго этажа (пом. 11)

Коридор второго этажа (пом. 11) · вид изнутри помещения · размеры в мм, отметки в м от ±0,000 (чистый пол 1-го этажа)


ПРЕДВАРИТЕЛЬНО · не для производства работ · открыто пунктов: 11 (реестр — л. 7–9)

Развёртка стены А

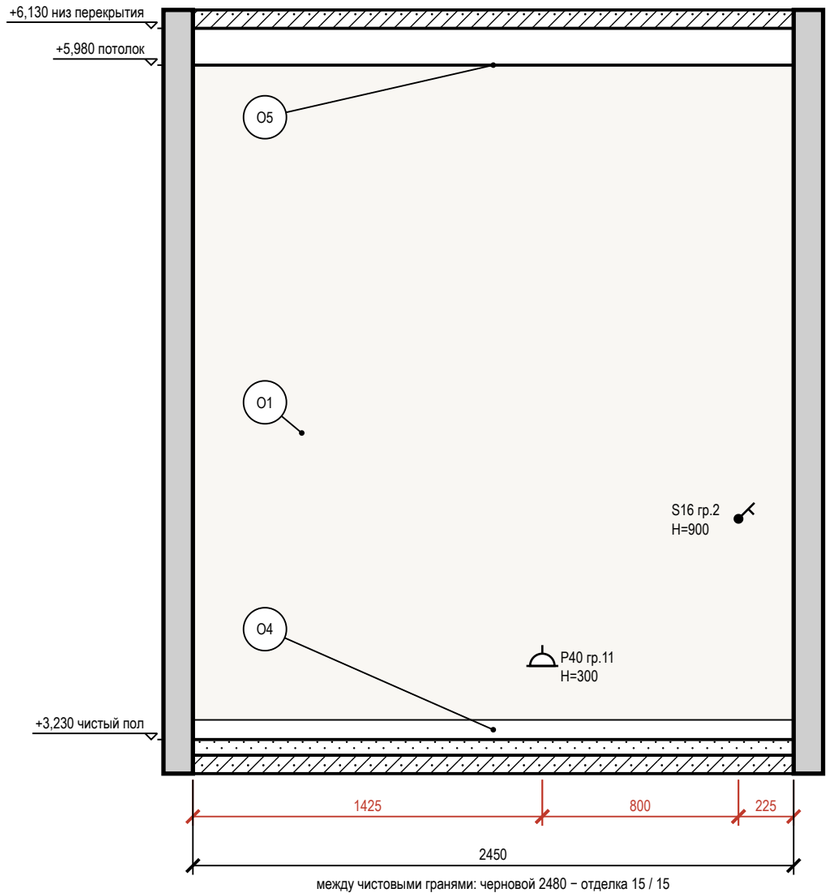

между чистовыми гранями: черновой 2480 − отделка 15 / 15

Развёртка стены В

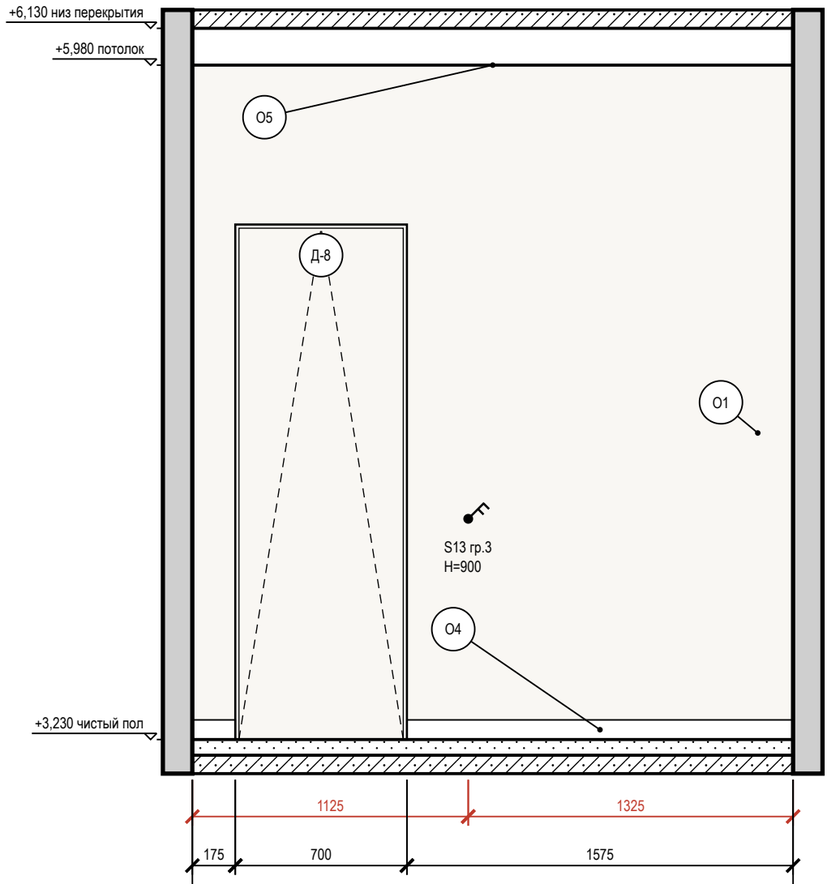

между чистовыми гранями: черновой 2480 − отделка 15 / 15

Условные обозначения

- розетка с заземляющим контактом; у знака — марка, ×N постов в рамке, гр. — группа щита, H — высота оси, мм
- выключатель одноклавишный
- выключатель двухклавишный (флажков — по числу клавиш)
- привязки точек и выводов от угла и от пола, мм
- мебель и приборы — фасад по расстановке (условно)
- дверь скрытого монтажа: полотно в плоскости стены (узел — на листе узлов)
- стены и перекрытия в сечении
- окраска: тон — цвет по коду производителя (условно)
- О1 — марка отделки по реестру отделки альбома
- A — марка развёртки: буква стены, стрелка — взгляд


Допущения и предложения на листе

Основа листа: взаимное расположение помещений, контур дома 9600 × 8000 и раскладка этажей подобраны проектировщиком под габариты помещений брифа; обмер и проект АР — задание (К-1); высота потолка 2900 мм — по брифу, не замерена; перекрытие 330 мм и отметка 2-го этажа +3,230 приняты; проект КР — задание (К-2); наружные стены 400 мм, перегородки 120 мм приняты (в брифе толщин нет) (К-1); разрешённая мощность 15 кВт принята по типовым ТУ для частного дома (К-4); подрайон климата не задан — принят не северный (жилые от 2,5 м) (К-7).

Знак «*» — принято, не замерено и не подтверждено (замерить на объекте): К-1: дверь пом. 11 (стена Б) — проём: место и ширина приняты проектировщиком по брифу (раскладка этажей — К-1), не замерены; К-2: отметка чистого пола этажа «2-й этаж» +3,230 — отметка чистого пола 2-го этажа +3,230 принята: высота потолка 2900 по брифу + перекрытие с полом 330 (конструкция перекрытия не задана; проект КР — задание).

См. лист открытых вопросов (лист 7, записи К-1, К-2, К-4; лист 8, запись К-7).

Схема развёрток (М 1:100)

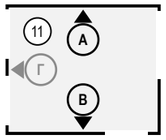

Ведомость отделки (на листе)

Марка	Поверхность	Материал, изделие	Цвет, код	Кол.
О1	стены	окраска, Tikkurila, матовая, подготовка Q3	Tikkurila G503 «Calla»	12 м²
О4	плинтус	плинтус МДФ, h 80 мм, аналог: плинтус МДФ под покраску 80×16	Tikkurila G503 «Calla»	4,2 м
О5	потолок	окраска, Little Greene Absolute Matt, глубокоматовая, подготовка Q3	Little Greene No. 222 «Loft White»	5,2 м²

Примечания

1. Развёртки — вид на стену изнутри помещения, по часовой стрелке; расположение — на схеме листа и на листе 117; размеры — в мм по чистовым поверхностям; отметки — в м от ±0,000 (чистый пол 1-го этажа); высоты H — от чистого пола помещения до оси изделия, у декора — до центра.
2. Красная цепочка — привязки электроточек и выводов по осям от угла чистовых стен; высота H — у знака, от чистого пола до оси; высоты мебели, проёмов и границ отделки — колонкой отметок слева. Стена с 5 и более точками или с мелкими звеньями привязок показана двумя видами: архитектурная развёртка (мебель, отделка, проёмы, высоты) и вид «Привязки» на отдельном листе — точки и выводы с марками, одна цепочка по осям и таблица привязок (каждая точка — строка).
3. У знака электроточки: марка (Р — розетка, S — выключатель, Св — светильник, ЭВ — вывод кабеля), ×N — число постов в рамке, гр. — группа щита, H — высота оси от чистого пола, мм; группы по клавишам выключателя — на листе выключателей.
4. Схема мебели, приборов и декора не является технической документацией для производства мебели; габариты — по паспортам изделий.
5. Двери скрытого монтажа — полотно в плоскости стены, отделка стены по полотну, плинтус прерывается у короба (узел — на листе узлов).

1000 мм · печать 1:1

Изм.	Кол.уч	Лист	№ док.	Подп.	Дата
Разраб.		Кырлан А.С.			04.11.26
Пров.					
ГИП					
Н. контр.					
Утв.					

ГД-2026-012-АИ

Дом 120 м²

Общая площадь 147,36* м² · * размеры приняты, не замерены (реестр — л. 7–9, К-1)

Дизайн-проект интерьера	Стадия	Лист	Листов
	РП	158	175

Развёртки стен А, В. Коридор второго этажа (пом. 11)

М 1:25

Кырлан Александр Сергеевич


выпуск 04.11.2026 № 4dfa962484 · стр. 162 из 180

Развёртка стены Г. Коридор второго этажа (пом. 11)

Коридор второго этажа (пом. 11) · вид изнутри помещения · размеры в мм, отметки в м от ±0,000 (чистый пол 1-го этажа)


ПРЕДВАРИТЕЛЬНО · не для производства работ · открыто пунктов: 11 (реестр — л. 7–9)

Развёртка стены Г

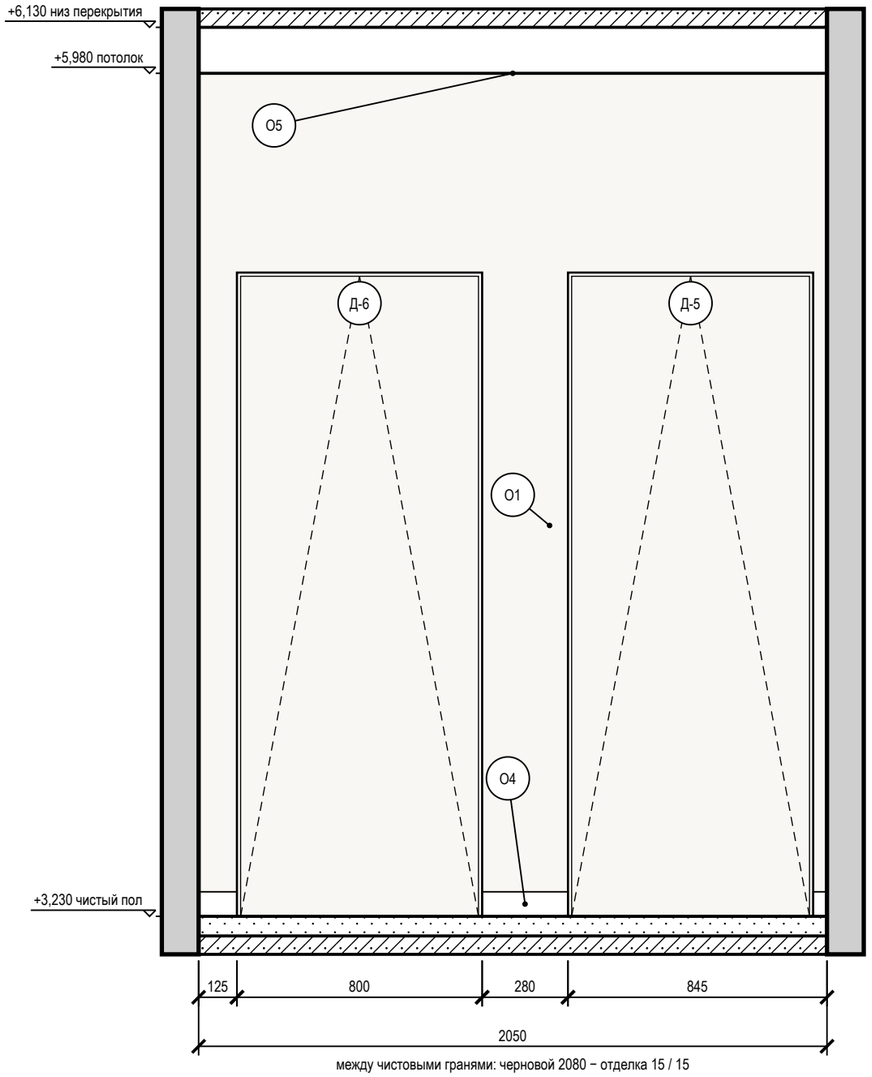

между чистовыми гранями: черновой 2080 − отделка 15 / 15

Схема развёрток (М 1:100)

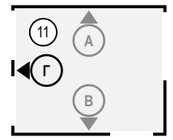

Условные обозначения

- мебель и приборы — фасад по расстановке (условно)
- дверь скрытого монтажа: полотно в плоскости стены (узел — на листе узлов)
- стены и перекрытия в сечении
- окраска: тон — цвет по коду производителя (условно)
- О1 — марка отделки по реестру отделки альбома
- А — марка развёртки: буква стены, стрелка — взгляд

Ведомость отделки (на листе)

Марка	Поверхность	Материал, изделие	Цвет, код	Кол.
О1	стены	окраска, Tikkurila, матовая, подготовка Q3	Tikkurila G503 «Calla»	2,3 м²
О4	плинтус	плинтус МДФ, h 80 мм, аналог: плинтус МДФ под покраску 80×16	Tikkurila G503 «Calla»	0,5 м
О5	потолок	окраска, Little Greene Absolute Matt, глубокоматовая, подготовка Q3	Little Greene No. 222 «Loft White»	5,2 м²

Допущения и предложения на листе

Основа листа: взаимное расположение помещений, контур дома 9600 × 8000 и раскладка этажей подобраны проектировщиком под габариты помещений брифа; обмер и проект АР — задание (К-1); высота потолка 2900 мм — по брифу, не замерена; перекрытие 330 мм и отметка 2-го этажа +3,230 приняты; проект КР — задание (К-2); наружные стены 400 мм, перегородки 120 мм приняты (в брифе толщин нет) (К-1); разрешённая мощность 15 кВт принята по типовым ТУ для частного дома (К-4); подрайон климата не задан — принят не северный (жилые от 2,5 м) (К-7).
Знак «*» — принято, не замерено и не подтверждено (замерить на объекте): К-1: дверь пом. 11 (стена Б) — проём: место и ширина приняты проектировщиком по брифу (раскладка этажей — К-1), не замерены; К-2: отметка чистого пола этажа «2-й этаж» +3,230 — отметка чистого пола 2-го этажа +3,230 принята: высота потолка 2900 по брифу + перекрытие с полом 330 (конструкция перекрытия не задана; проект КР — задание).
См. лист открытых вопросов (лист 7, записи К-1, К-2, К-4; лист 8, запись К-7).

Примечания

1. Развёртки — вид на стену изнутри помещения, по часовой стрелке; расположение — на схеме листа и на листе 117; размеры — в мм по чистовым поверхностям; отметки — в м от ±0,000 (чистый пол 1-го этажа); высоты Н — от чистого пола помещения до оси изделия, у декора — до центра.
2. Схема мебели, приборов и декора не является технической документацией для производства мебели; габариты — по паспортам изделий.
3. Двери скрытого монтажа — полотно в плоскости стены, отделка стены по полотну, плинтус прерывается у короба (узел — на листе узлов).

1000 мм · печать 1:1

Изм.	Кол.уч	Лист	№ док.	Подп.	Дата
Разраб.		Кырлан А.С.			04.11.26
Пров.					
ГИП					
Н. контр.					
Утв.					

ГД-2026-012-АИ

Дом 120 м²

Общая площадь 147,36* м² · * размеры приняты, не замерены (реестр — л. 7–9, К-1)

Дизайн-проект интерьера

Стадия	Лист	Листов
РП	159	175

Развёртка стены Г. Коридор второго этажа (пом. 11)

М 1:20

Кырлан Александр Сергеевич


выпуск 04.11.2026 № 4dfa962484 · стр. 163 из 180

Развёртка стены А. Детская вторая (пом. 12)

Детская вторая (пом. 12) · вид изнутри помещения · размеры в мм, отметки в м от ±0,000 (чистый пол 1-го этажа)


ПРЕДВАРИТЕЛЬНО · не для производства работ · открыто пунктов: 11 (реестр — л. 7–9)

Развёртка стены А

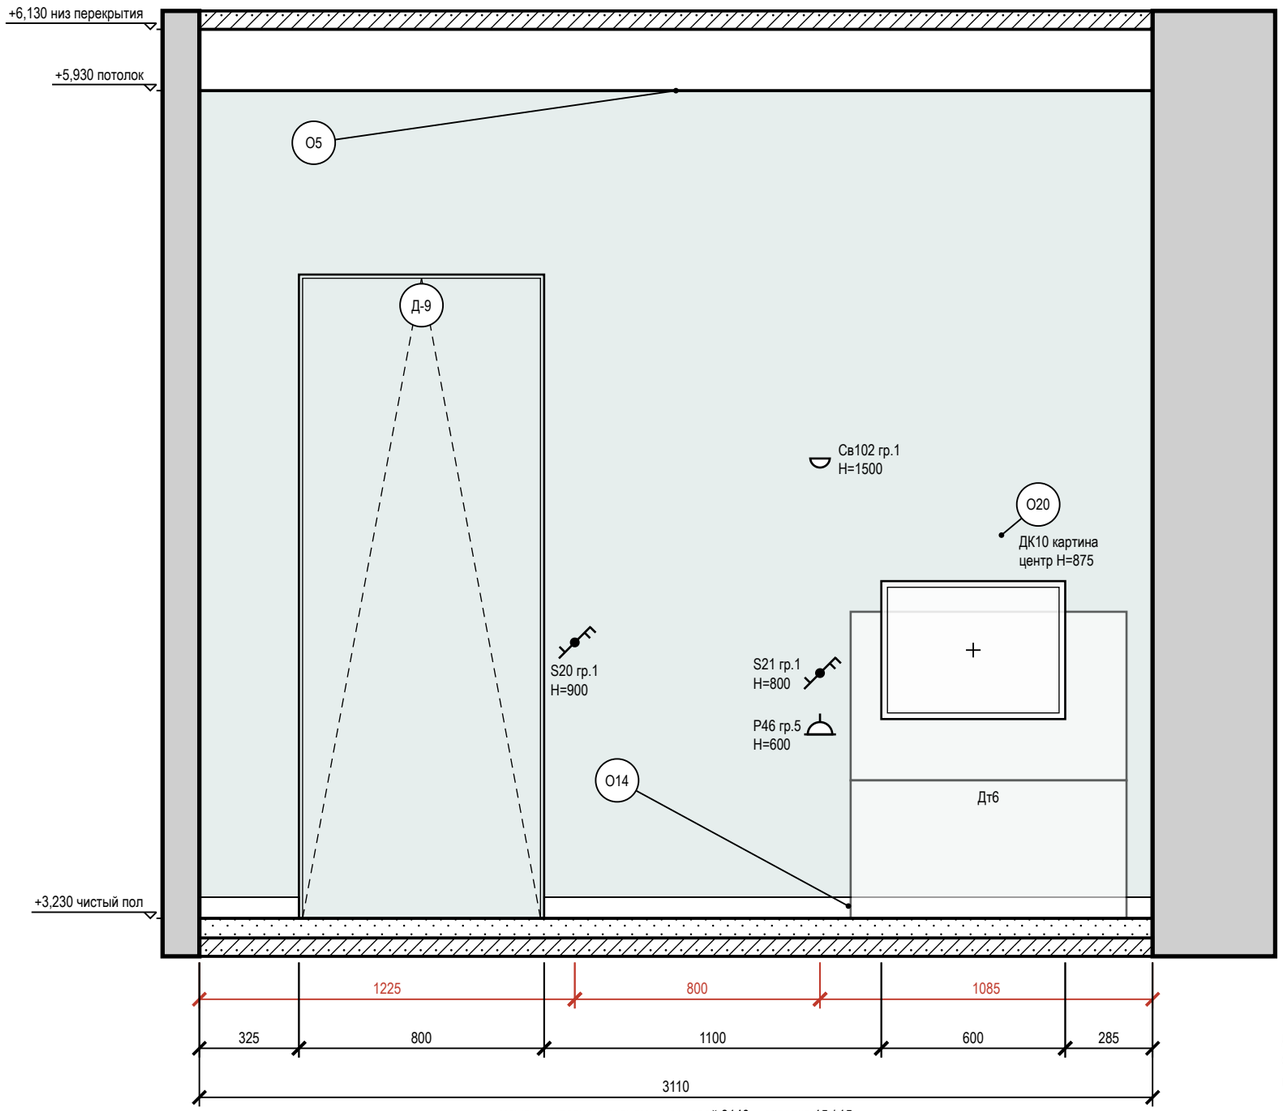

между чистовыми гранями: черновой 3140 − отделка 15 / 15

Схема развёрток (М 1:100)

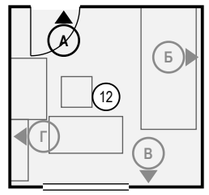

Условные обозначения

- розетка с заземляющим контактом; у знака — марка, ×N постов в рамке, гр. — группа щита, Н — высота оси, мм
- выключатель одноклавишный
- выключатель двухклавишный (флажков — по числу клавиш)
- выключатель с проходной или перекрёстной клавишей (обратный флажок); тип клавиши — в подписи
- светильник настенный (бра), Н — высота оси
- привязки точек и выводов от угла и от пола, мм
- мебель и приборы — фасад по расстановке (условно)
- картина (декор): марка Д, крест — центр, Н — высота центра, мм
- дверь скрытого монтажа: полотно в плоскости стены (узел — на листе узлов)
- стены и перекрытия в сечении
- окраска: тон — цвет по коду производителя (условно)
- О1 — марка отделки по реестру отделки альбома
- А — марка развёртки: буква стены, стрелка — взгляд

Ведомость отделки (на листе)

Марка	Поверхность	Материал, изделие	Цвет, код	Кол.
О5	потолок	окраска, Little Greene Absolute Matt, глубокоматовая, подготовка Q3	Little Greene No. 222 «Loft White»	9,2 м²
О14	плинтус	плинтус МДФ, Orac Decor Contour (Luxxus), h 69 мм, SX165	Tikkurila G503 «Calla»	2,3 м
О20	акцентная стена	окраска, Tikkurila, шелковисто-матовая, подготовка Q3	Tikkurila H440 «H440 Wave — бирюзово-голубая вода»	6,7 м²

Допущения и предложения на листе

Основа листа: взаимное расположение помещений, контур дома 9600 × 8000 и раскладка этажей подобраны проектировщиком под габариты помещений брифа; обмер и проект АР — задание (К-1); высота потолка 2900 мм — по брифу, не замерена; перекрытие 330 мм и отметка 2-го этажа +3,230 приняты; проект КР — задание (К-2); наружные стены 400 мм, перегородки 120 мм приняты (в брифе толщин нет) (К-1); разрешённая мощность 15 кВт принята по типовым ТУ для частного дома (К-4); подрайон климата не задан — принят не северный (жилые от 2,5 м) (К-7).
Знак «*» — принято, не замерено и не подтверждено (замерить на объекте): К-1: окно пом. 12 (стена В) — окно: место, ширина, высота и подоконник приняты по брифу, стена — по раскладке проектировщика (К-1), не замерены; дверь пом. 12 (стена А) — проём: место и ширина приняты проектировщиком по брифу (раскладка этажей — К-1), не замерены; К-2: отметка чистого пола этажа «2-й этаж» +3,230 — отметка чистого пола 2-го этажа +3,230 принята: высота потолка 2900 по брифу + перекрытие с полом 330 (конструкция перекрытия не задана; проект КР — задание).
См. лист открытых вопросов (лист 7, записи К-1, К-2, К-4; лист 8, запись К-7).

Примечания

1. Развёртки — вид на стену изнутри помещения, по часовой стрелке; расположение — на схеме листа и на листе 117; размеры — в мм по чистовым поверхностям; отметки — в м от ±0,000 (чистый пол 1-го этажа); высоты Н — от чистого пола помещения до оси изделия, у декора — до центра.
2. Красная цепочка — привязки электроточек и выводов по осям от угла чистовых стен; высота Н — у знака, от чистого пола до оси; высоты мебели, проёмов и границ отделки — колонкой отметок слева. Стена с 5 и более точками или с мелкими звеньями привязок показана двумя видами: архитектурная развёртка (мебель, отделка, проёмы, высоты) и вид «Привязки» на отдельном листе — точки и выводы с марками, одна цепочка по осям и таблица привязок (каждая точка — строка).
3. У знака электроточки: марка (Р — розетка, S — выключатель, Св — светильник, ЭВ — вывод кабеля), ×N — число постов в рамке, гр. — группа щита, Н — высота оси от чистого пола, мм; группы по клавишам выключателя — на листе выключателей.
4. Схема мебели, приборов и декора не является технической документацией для производства мебели; габариты — по паспортам изделий.
5. Картины и зеркала крепить к основанию по паспорту изделия (закладные и анкеры — в перечне скрытых работ); крест — ось центра предмета.
6. Двери скрытого монтажа — полотно в плоскости стены, отделка стены по полотну, плинтус прерывается у короба (узел — на листе узлов).
7. Потолок — у каждой стены свой, по плану потолков (ПТ8); ступени — зоной, кромка короба перед нишей — тонкой линией; в поле потолка: ПТ7 +6,030.

1000 мм · печать 1:1

Изм.	Кол.уч	Лист	№ док.	Подп.	Дата				
Разраб.		Кырлан А.С.			04.11.26	**ГД-2026-012-АИ**			
Пров.						Дом 120 м²			
ГИП						Общая площадь 147,36* м² · * размеры приняты, не замерены (реестр — л. 7–9, К-1)			
						Дизайн-проект интерьера	Стадия	Лист	Листов
Н. контр.							РП	160	175
Утв.						**Развёртка стены А. Детская вторая (пом. 12)** М 1:20	**Кырлан Александр Сергеевич**		

Развёртка стены Б. Детская вторая (пом. 12)

Детская вторая (пом. 12) · вид изнутри помещения · размеры в мм, отметки в м от ±0,000 (чистый пол 1-го этажа)

ПРЕДВАРИТЕЛЬНО · не для производства работ · открыто пунктов: 11 (реестр — л. 7–9)

Развёртка стены Б


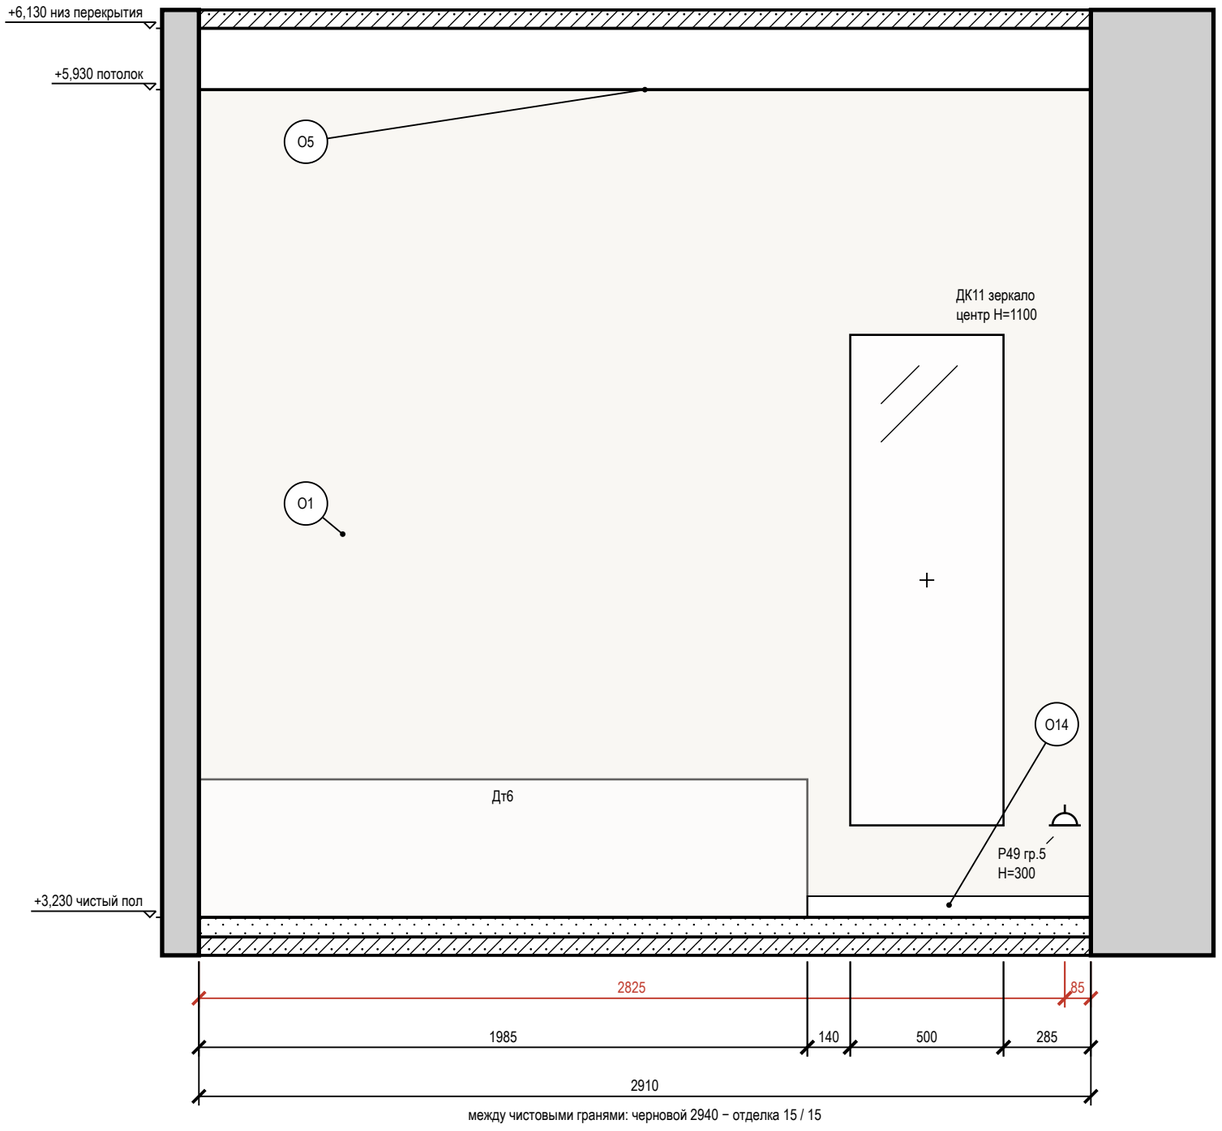


Схема развёрток (М 1:100)

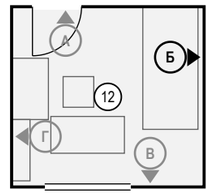

Условные обозначения

- розетка с заземляющим контактом; у знака — марка, ×N постов в рамке, гр. — группа щита, Н — высота оси, мм
- привязки точек и выводов от угла и от пола, мм
- мебель и приборы — фасад по расстановке (условно)
- зеркало: марка Д, крест — центр, Н — высота центра, мм
- стены и перекрытия в сечении
- окраска: тон — цвет по коду производителя (условно)
- О1 — марка отделки по реестру отделки альбома
- А — марка развёртки: буква стены, стрелка — взгляд

Ведомость отделки (на листе)

Марка	Поверхность	Материал, изделие	Цвет, код	Кол.
О1	стены	окраска, Tikkurila, шелковисто-матовая, подготовка Q3	Tikkurila G503 «Calla»	7,9 м²
О5	потолок	окраска, Little Greene Absolute Matt, глубокоматовая, подготовка Q3	Little Greene No. 222 «Loft White»	9,2 м²
О14	плинтус	плинтус МДФ, Orac Decor Contour (Luxxus), h 69 мм, SX165	Tikkurila G503 «Calla»	0,9 м

Допущения и предложения на листе. Основа листа: взаимное расположение помещений, контур дома 9600 × 8000 и раскладка этажей подобраны проектировщиком под габариты помещений брифа; обмер и проект АР — задание (К-1); высота потолка 2900 мм — по брифу, не замерена; перекрытие 330 мм и отметка 2-го этажа +3,230 приняты; проект КР — задание (К-2); наружные стены 400 мм, перегородки 120 мм приняты (в брифе толщин нет) (К-1); разрешённая мощность 15 кВт принята по типовым ТУ для частного дома (К-4); подрайон климата не задан — принят не северный (жилые от 2,5 м) (К-7). Знак «*» — принято, не замерено (замерить): К-1: окно пом. 12 (стена В), дверь пом. 12 (стена А); К-2: отметка чистого пола этажа «2-й этаж» +3,230. См. лист открытых вопросов (лист 7, записи К-1, К-2, К-4; лист 8, запись К-7).

Примечания

1. Развёртки — вид на стену изнутри помещения, по часовой стрелке; расположение — на схеме листа и на листе 117; размеры — в мм по чистовым поверхностям; отметки — в м от ±0,000 (чистый пол 1-го этажа); высоты Н — от чистого пола помещения до оси изделия, у декора — до центра.
2. Красная цепочка — привязки электроточек и выводов по осям от угла чистовых стен; высота Н — у знака, от чистого пола до оси; высоты мебели, проёмов и границ отделки — колонкой отметок слева. Стена с 5 и более точками или с мелкими звеньями привязок показана двумя видами: архитектурная развёртка (мебель, отделка, проёмы, высоты) и вид «Привязки» на отдельном листе — точки и выводы с марками, одна цепочка по осям и таблица привязок (каждая точка — строка).
3. У знака электроточки: марка (Р — розетка, S — выключатель, Св — светильник, ЭВ — вывод кабеля), ×N — число постов в рамке, гр. — группа щита, Н — высота оси от чистого пола, мм; группы по клавишам выключателя — на листе выключателей.
4. Схема мебели, приборов и декора не является технической документацией для производства мебели; габариты — по паспортам изделий.
5. Картины и зеркала крепить к основанию по паспорту изделия (закладные и анкеры — в перечне скрытых работ); крест — ось центра предмета.
6. Потолок — у каждой стены свой, по плану потолков (ПТ8); ступени — зоной, кромка короба перед нишей — тонкой линией; в поле потолка: ПТ7 +6,030.

1000 мм · печать 1:1

Изм.	Кол.уч	Лист	№ док.	Подп.	Дата
Разраб.		Кырлан А.С.			04.11.26
Пров.					
ГИП					
Н. контр.					
Утв.					

ГД-2026-012-АИ

Дом 120 м²

Общая площадь 147,36* м² · * размеры приняты, не замерены (реестр — л. 7–9, К-1)

Дизайн-проект интерьера

Стадия	Лист	Листов
РП	161	175

Развёртка стены Б. Детская вторая (пом. 12)

М 1:20


Кырлан Александр Сергеевич

Развёртка стены В. Детская вторая (пом. 12)

Детская вторая (пом. 12) · вид изнутри помещения · размеры в мм, отметки в м от ±0,000 (чистый пол 1-го этажа)


ПРЕДВАРИТЕЛЬНО · не для производства работ · открыто пунктов: 11 (реестр — л. 7–9)

Развёртка стены В

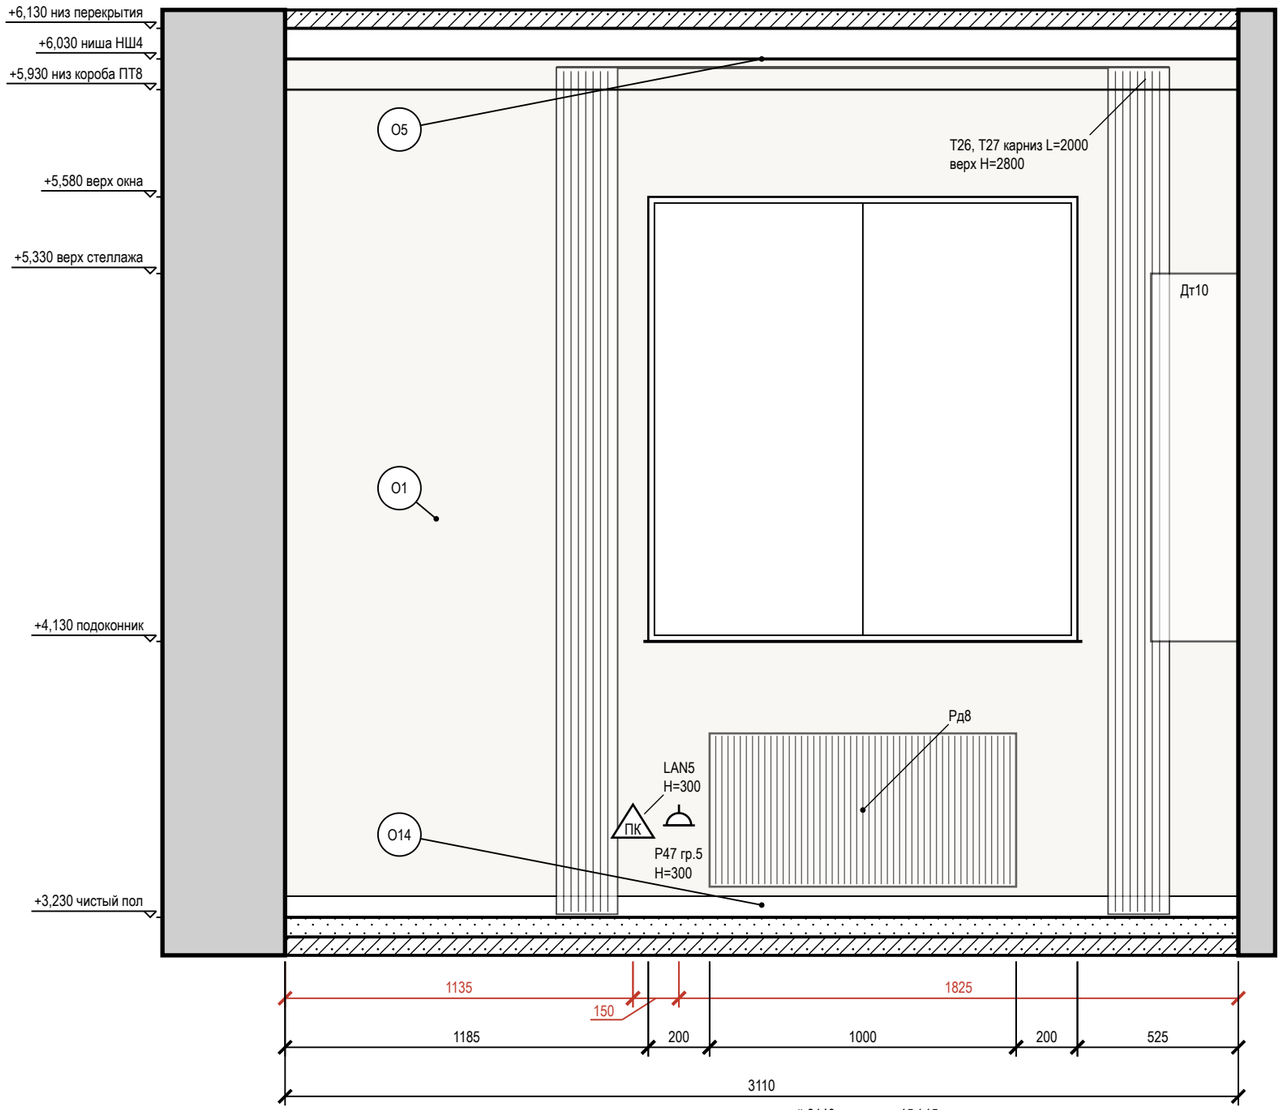

между чистовыми гранями: черновой 3140 − отделка 15 / 15

Схема развёрток (М 1:100)

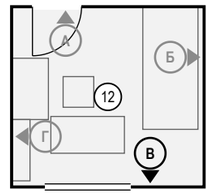

Условные обозначения

- розетка с заземляющим контактом; у знака — марка, ×N постов в рамке, гр. — группа щита, H — высота оси, мм
- ПК — розетка компьютерная RJ45
- привязки точек и выводов от угла и от пола, мм
- мебель и приборы — фасад по расстановке (условно)
- карниз (шина) и шторы в собранном виде: марка Т, длина L, верх H
- окно: проём, рама, подоконник
- радиатор отопления; марка — по плану отопления
- стены и перекрытия в сечении
- окраска: тон — цвет по коду производителя (условно)
- О1 — марка отделки по реестру отделки альбома
- А — марка развёртки: буква стены, стрелка — взгляд

Ведомость отделки (на листе)

Марка	Поверхность	Материал, изделие	Цвет, код	Кол.
О1	стены	окраска, Tikkurila, шелковисто-матовая, подготовка Q3	Tikkurila G503 «Calla»	6,7 м²
О5	потолок	окраска, Little Greene Absolute Matt, глубокоматовая, подготовка Q3	Little Greene No. 222 «Loft White»	9,2 м²
О14	плинтус	плинтус МДФ, Orac Decor Contour (Luxxus), h 69 мм, SX165	Tikkurila G503 «Calla»	3,1 м

Допущения и предложения на листе. Основа листа: взаимное расположение помещений, контур дома 9600 × 8000 и раскладка этажей подобраны проектировщиком под габариты помещений брифа; обмер и проект АР — задание (К-1); высота потолка 2900 мм — по брифу, не замерена; перекрытие 330 мм и отметка 2-го этажа +3,230 приняты; проект КР — задание (К-2); наружные стены 400 мм, перегородки 120 мм приняты (в брифе толщин нет) (К-1); разрешённая мощность 15 кВт принята по типовым ТУ для частного дома (К-4); подрайон климата не задан — принят не северный (жилые от 2,5 м) (К-7). Знак «*» — принято, не замерено (замерить): К-1: окно пом. 12 (стена В), дверь пом. 12 (стена А); К-2: отметка чистого пола этажа «2-й этаж» +3,230. См. лист открытых вопросов (лист 7, записи К-1, К-2, К-4; лист 8, запись К-7; лист 9, запись ИЗ-2).

Примечания

1. Развёртки — вид на стену изнутри помещения, по часовой стрелке; расположение — на схеме листа и на листе 117; размеры — в мм по чистовым поверхностям; отметки — в м от ±0,000 (чистый пол 1-го этажа); высоты H — от чистого пола помещения до оси изделия, у декора — до центра.
2. Красная цепочка — привязки электроточек и выводов по осям от угла чистовых стен; высота H — у знака, от чистого пола до оси; высоты мебели, проёмов и границ отделки — колонкой отметок слева. Стена с 5 и более точками или с мелкими звеньями привязок показана двумя видами: архитектурная развёртка (мебель, отделка, проёмы, высоты) и вид «Привязки» на отдельном листе — точки и выводы с марками, одна цепочка по осям и таблица привязок (каждая точка — строка).
3. У знака электроточки: марка (Р — розетка, S — выключатель, Св — светильник, ЭВ — вывод кабеля), ×N — число постов в рамке, гр. — группа щита, H — высота оси от чистого пола, мм; группы по клавишам выключателя — на листе выключателей.
4. Схема мебели, приборов и декора не является технической документацией для производства мебели; габариты — по паспортам изделий.
5. Карнизы (шины) — по ведомости текстиля декоратора: длина L и верх H на развёртке — те же числа, что в ведомости; крепление — до окраски потолка.
6. Потолок — у каждой стены свой, по плану потолков (НШ4, ПТ8); ступени — зоной, кромка короба перед нишей — тонкой линией; в поле потолка: ПТ7 +6,030.

1000 мм · печать 1:1

Изм.	Кол.уч	Лист	№ док.	Подп.	Дата
Разраб.		Кырлан А.С.			04.11.26
Пров.					
ГИП					
Н. контр.					
Утв.					

ГД-2026-012-АИ

Дом 120 м²

Общая площадь 147,36* м² · * размеры приняты, не замерены (реестр — л. 7–9, К-1)

Дизайн-проект интерьера

Стадия	Лист	Листов
РП	162	175

Развёртка стены В. Детская вторая (пом. 12)

М 1:20

Кырлан Александр Сергеевич


выпуск 04.11.2026 № 4dfa962484 · стр. 166 из 180

Развёртка стены Г. Детская вторая (пом. 12)

Детская вторая (пом. 12) · вид изнутри помещения · размеры в мм, отметки в м от ±0,000 (чистый пол 1-го этажа)


ПРЕДВАРИТЕЛЬНО · не для производства работ · открыто пунктов: 11 (реестр — л. 7–9)

Развёртка стены Г

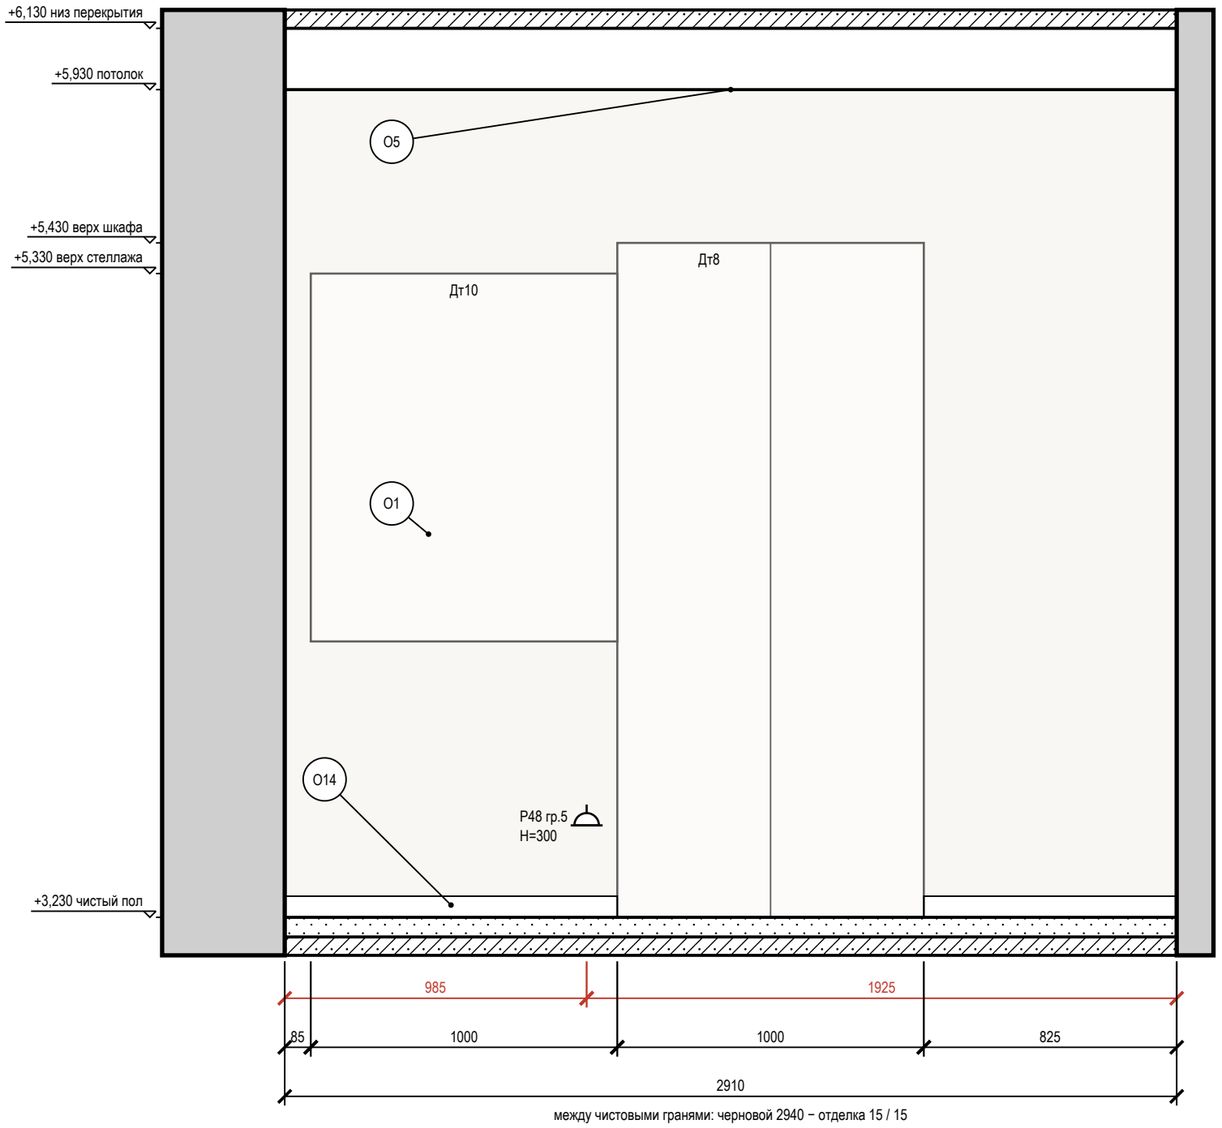

между чистовыми гранями: черновой 2940 − отделка 15 / 15

Схема развёрток (М 1:100)

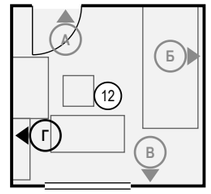

Условные обозначения

- розетка с заземляющим контактом; у знака — марка, ×N постов в рамке, гр. — группа щита, Н — высота оси, мм
- привязки точек и выводов от угла и от пола, мм
- мебель и приборы — фасад по расстановке (условно)
- стены и перекрытия в сечении
- окраска: тон — цвет по коду производителя (условно)
- О1 — марка отделки по реестру отделки альбома
- А — марка развёртки: буква стены, стрелка — взгляд

Ведомость отделки (на листе)

Марка	Поверхность	Материал, изделие	Цвет, код	Кол.
О1	стены	окраска, Tikkurila, шелковисто-матовая, подготовка Q3	Tikkurila G503 «Calla»	7,9 м²
О5	потолок	окраска, Little Greene Absolute Matt, глубокоматовая, подготовка Q3	Little Greene No. 222 «Loft White»	9,2 м²
О14	плинтус	плинтус МДФ, Orac Decor Contour (Luxxus), h 69 мм, SX165	Tikkurila G503 «Calla»	1,9 м

Допущения и предложения на листе. Основа листа: взаимное расположение помещений, контур дома 9600 × 8000 и раскладка этажей подобраны проектировщиком под габариты помещений брифа; обмер и проект АР — задание (К-1); высота потолка 2900 мм — по брифу, не замерена; перекрытие 330 мм и отметка 2-го этажа +3,230 приняты; проект КР — задание (К-2); наружные стены 400 мм, перегородки 120 мм приняты (в брифе толщин нет) (К-1); разрешённая мощность 15 кВт принята по типовым ТУ для частного дома (К-4); подрайон климата не задан — принят не северный (жилые от 2,5 м) (К-7). Знак «*» — принято, не замерено (замерить): К-1: окно пом. 12 (стена В), дверь пом. 12 (стена А); К-2: отметка чистого пола этажа «2-й этаж» +3,230. См. лист открытых вопросов (лист 7, записи К-1, К-2, К-4; лист 8, запись К-7).

Примечания

1. Развёртки — вид на стену изнутри помещения, по часовой стрелке; расположение — на схеме листа и на листе 117; размеры — в мм по чистовым поверхностям; отметки — в м от ±0,000 (чистый пол 1-го этажа); высоты Н — от чистого пола помещения до оси изделия, у декора — до центра.
2. Красная цепочка — привязки электроточек и выводов по осям от угла чистовых стен; высота Н — у знака, от чистого пола до оси; высоты мебели, проёмов и границ отделки — колонкой отметок слева. Стена с 5 и более точками или с мелкими звеньями привязок показана двумя видами: архитектурная развёртка (мебель, отделка, проёмы, высоты) и вид «Привязки» на отдельном листе — точки и выводы с марками, одна цепочка по осям и таблица привязок (каждая точка — строка).
3. У знака электроточки: марка (Р — розетка, S — выключатель, Св — светильник, ЭВ — вывод кабеля), ×N — число постов в рамке, гр. — группа щита, Н — высота оси от чистого пола, мм; группы по клавишам выключателя — на листе выключателей.
4. Схема мебели, приборов и декора не является технической документацией для производства мебели; габариты — по паспортам изделий.
5. Потолок — у каждой стены свой, по плану потолков (ПТ8); ступени — зоной, кромка короба перед нишей — тонкой линией; в поле потолка: ПТ7 +6,030.

1000 мм · печать 1:1

Изм.	Кол.уч	Лист	№ док.	Подп.	Дата
Разраб.		Кырлан А.С.			04.11.26
Пров.					
ГИП					
Н. контр.					
Утв.					

ГД-2026-012-АИ

Дом 120 м²

Общая площадь 147,36* м² · * размеры приняты, не замерены (реестр — л. 7–9, К-1)

Дизайн-проект интерьера

Стадия	Лист	Листов
РП	163	175

Развёртка стены Г. Детская вторая (пом. 12)

М 1:20

Кырлан Александр Сергеевич


выпуск 04.11.2026 № 4dfa962484 · стр. 167 из 180

Развёртки стен А, Б. Санузел второго этажа (пом. 13)

Санузел второго этажа (пом. 13) · вид изнутри помещения · размеры в мм, отметки в м от ±0,000 (чистый пол 1-го этажа)


ПРЕДВАРИТЕЛЬНО · не для производства работ · открыто пунктов: 11 (реестр — л. 7–9)

Развёртка стены А

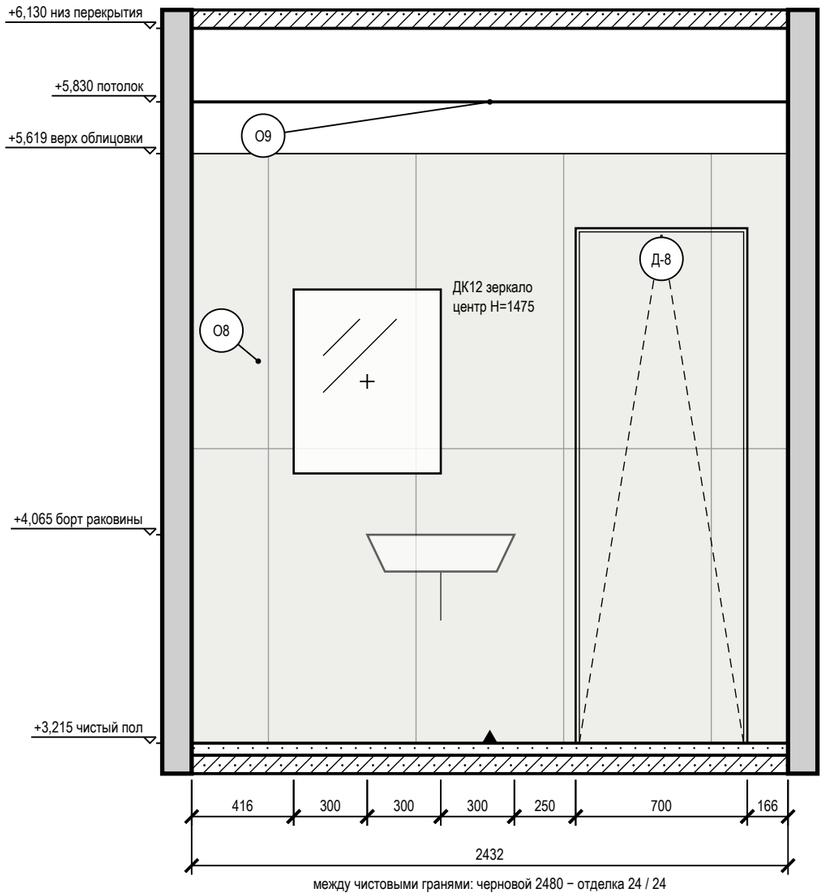

между чистовыми гранями: черновой 2480 − отделка 24 / 24

Развёртка стены Б

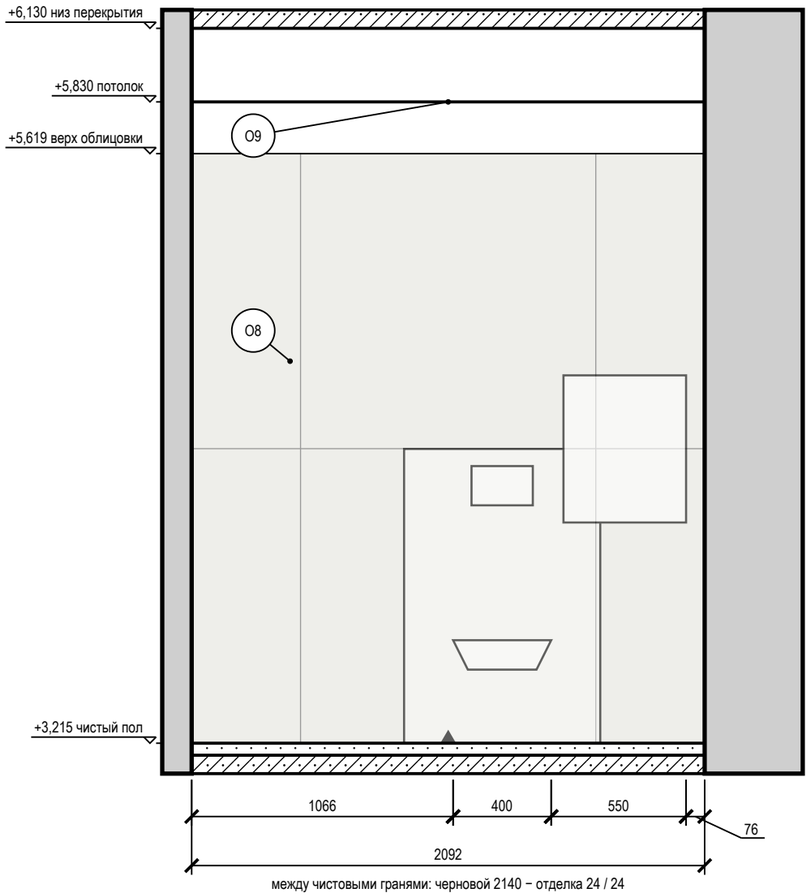


между чистовыми гранями: черновой 2140 − отделка 24 / 24

Условные обозначения

- мебель и приборы — фасад по расстановке (условно)
- зеркало: марка Д, крест — центр, Н — высота центра, мм
- дверь скрытого монтажа: полотно в плоскости стены (узел — на листе узлов)
- стены и перекрытия в сечении
- плитка: сетка швов по формату, ▲ — ось старта
- О1 — марка отделки по реестру отделки альбома
- А — марка развёртки: буква стены, стрелка — взгляд

Схема развёрток (М 1:100)

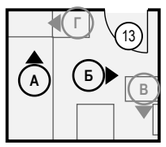

Ведомость отделки (на листе)

Марка	Поверхность	Материал, изделие	Цвет, код	Кол.
О8	стены	облицовка плиткой, Atlas Concorde Marvel Travertine, 600×1200×9 мм, A8UZ, затирка CG2WA	Atlas Concorde A8UZ «Marvel Travertine»	9,4 м²
О9	потолок	окраска, Little Greene Intelligent Bathroom, матовая, подготовка Q3	Little Greene No. 222 «Loft White»	5,3 м²

Допущения и предложения на листе

Основа листа: взаимное расположение помещений, контур дома 9600 × 8000 и раскладка этажей подобраны проектировщиком под габариты помещений брифа; обмер и проект АР — задание (К-1); высота потолка 2900 мм — по брифу, не замерена; перекрытие 330 мм и отметка 2-го этажа +3,230 приняты; проект КР — задание (К-2); наружные стены 400 мм, перегородки 120 мм приняты (в брифе толщин нет) (К-1); разрешённая мощность 15 кВт принята по типовым ТУ для частного дома (К-4); подрайон климата не задан — принят не северный (жилые от 2,5 м) (К-7).

Знак «*» — принято, не замерено и не подтверждено (замерить на объекте): К-1: дверь пом. 13 (стена А) — Петли у правого откоса (х 6150, у стояков): открытое полотно стоит вдоль стены Б, вошедший идёт влево к умывальнику и ванне; К-2: отметка чистого пола этажа «2-й этаж» +3,230 — отметка чистого пола 2-го этажа +3,230 принята: высота потолка 2900 по брифу + перекрытие с полом 330 (конструкция перекрытия не задана; проект КР — задание).

См. лист открытых вопросов (лист 7, записи К-1, К-2, К-4; лист 8, запись К-7).

Примечания

1. Развёртки — вид на стену изнутри помещения, по часовой стрелке; расположение — на схеме листа и на листе 117; размеры — в мм по чистовым поверхностям; отметки — в м от ±0,000 (чистый пол 1-го этажа); высоты Н — от чистого пола помещения до оси изделия, у декора — до центра.
2. Стены А, Б показаны двумя видами: здесь — архитектурная развёртка (мебель, отделка, проёмы, высоты), электроточки и выводы ВК с привязками и таблицей — на листах 165, 166 («Привязки»).
3. Схема мебели, приборов и декора не является технической документацией для производства мебели; габариты — по паспортам изделий (* — высота не задана в проекте, показана по типовому изделию).
4. Облицовка — по сетке швов 2 мм, раскладка от оси стены (треугольник у пола), целые ряды от пола; подрезки — по листу раскладки плитки.
5. Гидроизоляция в 2 слоя, заход на стены 200 мм; над ванной — до 2000 и 300 мм за борт — до облицовки, с актом скрытых работ и тестом проливом (узел — на листе узлов).
6. Картины и зеркала крепить к основанию по паспорту изделия (закладные и анкеры — в перечне скрытых работ); крест — ось центра предмета.
7. Двери скрытого монтажа — полотно в плоскости стены, отделка стены по полотну, плинтус прерывается у короба (узел — на листе узлов).

1000 мм · печать 1:1

Изм.	Кол.уч	Лист	№ док.	Подп.	Дата
Разраб.		Кырлан А.С.			04.11.26
Пров.					
ГИП					
Н. контр.					
Утв.					

ГД-2026-012-АИ

Дом 120 м²

Общая площадь 147,36* м² · * размеры приняты, не замерены (реестр — л. 7–9, К-1)

Дизайн-проект интерьера

Стадия	Лист	Листов
РП	164	175

Развёртки стен А, Б. Санузел второго этажа (пом. 13)

М 1:25

Кырлан Александр Сергеевич

выпуск 04.11.2026 № 4dfa962484 · стр. 168 из 180

Привязки электроточек и выводов ВК, стена А. Санузел второго этажа (пом. 13)

Санузел второго этажа (пом. 13) · вид изнутри помещения · привязки в мм, отметки в м · к развёртке на листе 164

ПРЕДВАРИТЕЛЬНО · не для производства работ · открыто пунктов: 11 (реестр — л. 7–9)

Развёртка стены А: электроточки и выводы

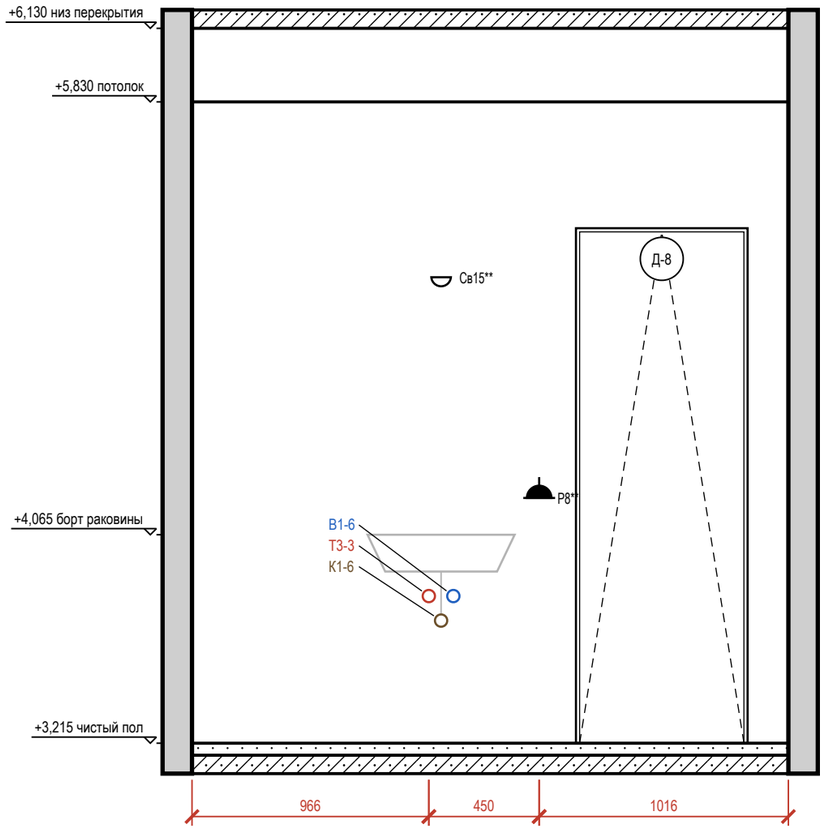



Таблица привязок электроточек и выводов

Марка	Назначение	От угла, мм	Н от пола, мм	Примечание
Т3-3	горячая вода — умывальник	966	600*	межос. 100
К1-6	канализация — умывальник	1016	500*	Ø50
Св15**	светильник настенный	1016	1900	гр. 3
В1-6	холодная вода — умывальник	1066	600*	межос. 100
Р8**	розетка: фен у умывальника	1416	1000	гр. 16, IP44

Условные обозначения

- розетка влагозащищённая IP44
- светильник настенный (бра), Н — высота оси
- вывод В1 (код — в ведомости привязок)
- вывод Т3 (код — в ведомости привязок)
- вывод К1 (код — в ведомости привязок)
- привязки точек и выводов от угла и от пола, мм
- марка развёртки: буква стены, стрелка — взгляд

Схема развёрток (М 1:50)

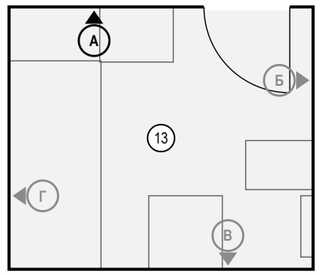

Допущения и предложения на листе

Основа листа: взаимное расположение помещений, контур дома 9600 × 8000 и раскладка этажей подобраны проектировщиком под габариты помещений брифа; обмер и проект АР — задание (К-1); высота потолка 2900 мм — по брифу, не замерена; перекрытие 330 мм и отметка 2-го этажа +3,230 приняты; проект КР — задание (К-2); наружные стены 400 мм, перегородки 120 мм приняты (в брифе толщин нет) (К-1); разрешённая мощность 15 кВт принята по типовым ТУ для частного дома (К-4); подрайон климата не задан — принят не северный (жилые от 2,5 м) (К-7).

Знак «*» — принято, не замерено и не подтверждено (замерить на объекте): К-1: дверь пом. 13 (стена А) — Петли у правого откоса (х 6150, у стояков): открытое полотно стоит вдоль стены Б, вошедший идёт влево к умывальнику и ванне; К-2: отметка чистого пола этажа «2-й этаж» +3,230 — отметка чистого пола 2-го этажа +3,230 принята: высота потолка 2900 по брифу + перекрытие с полом 330 (конструкция перекрытия не задана; проект КР — задание).

Знак «**» — предложение проектировщика, заказчиком не утверждено (согласовать с заказчиком): ИЗ-1: Св15 — Бра над умывальником См4 — по оси раковины (offset 1100); ИЗ-1, ИЗ-2: Р8 — Фен у умывальника См4 (800…1400 на стене А): справа от раковины, до откоса проёма Д-8 (1650) — 150 мм.

См. лист открытых вопросов (лист 7, записи К-1, К-2, К-4; лист 8, запись К-7; лист 9, записи ИЗ-1, ИЗ-2).

Примечания

1. Вид «Привязки» стены А — электроточки и выводы ВК; архитектурная развёртка (мебель, отделка, проёмы, высоты) — на листе 164, расположение — на листе 117. Мебель и приборы — подложкой для ориентира; их марки и обозначения мебели, проёмов и стен — там же.
2. Привязки — в мм: по горизонтали от левого чистового угла стены до оси изделия, Н — от чистого пола до оси; все точки — в таблице привязок. Красная цепочка — привязки по осям; точки ближе 150 мм одна к другой в цепочку не дробятся — их привязки только в таблице.
3. У знака — марка электроточки (Р — розетка, S — выключатель, Св — светильник, ЭВ — вывод кабеля); посты в рамке и группа щита — в графе «Примечание»; группы по клавишам выключателя — на листе выключателей.
4. Коды выводов ВК: В1 — холодная вода, Т3 — горячая вода, К1 — канализация; номер после дефиса — номер вывода на листе выводов сантехники; * — высота принята по типовой практике монтажа, окончательно — по паспорту прибора.

1000 мм · печать 1:1

Изм.	Кол.уч	Лист	№ док.	Подп.	Дата
Разраб.		Кырлан А.С.			04.11.26
Пров.					
ГИП					
Н. контр.					
Утв.					

ГД-2026-012-АИ

Дом 120 м²

Общая площадь 147,36* м² · * размеры приняты, не замерены (реестр — л. 7–9, К-1)

Дизайн-проект интерьера

Стадия	Лист	Листов
РП	165	175

Привязки электроточек и выводов ВК, стена А. Санузел второго этажа (пом. 13)

М 1:25

Кырлан Александр Сергеевич

выпуск 04.11.2026 № 4dfa962484 · стр. 169 из 180

Привязки электроточек и выводов ВК, стена Б. Санузел второго этажа (пом. 13)

Санузел второго этажа (пом. 13) · вид изнутри помещения · привязки в мм, отметки в м · к развёртке на листе 164

Развёртка стены Б: электроточки и выводы

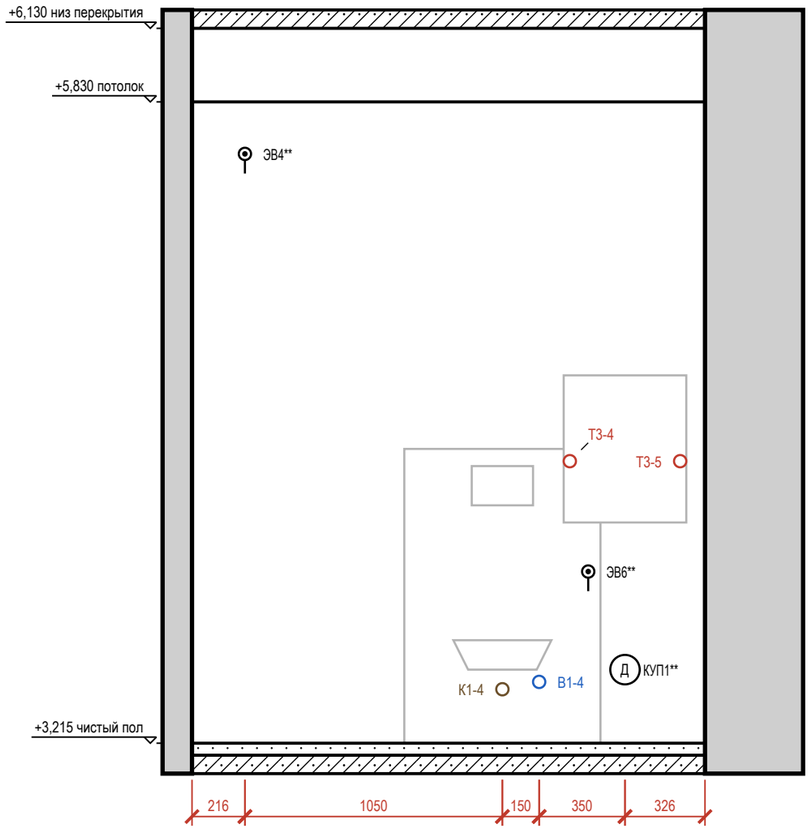



Таблица привязок электроточек и выводов

Марка	Назначение	От угла, мм	Н от пола, мм	Примечание
ЭВ4**	вывод кабеля: вентилятор ВР1 (таймер выбега)	216	2403	гр. 3
К1-4	канализация — унитаз подвесной	1266	220*	Ø110
В1-4	холодная вода — унитаз подвесной	1416	250*	в раме инсталляции
Т3-4	горячая вода — полотенцесушитель	1541	1150*	подача, межос. 450; байпас и краны
ЭВ6**	вывод кабеля: полотенцесушитель П10	1616	700	гр. 16
КУП1**	КУП — уравнивание потенциалов (ДСУП)	1766	300	
Т3-5	горячая вода — полотенцесушитель	1991	1150*	обратка

Условные обозначения

- вывод кабеля для подключения прибора (без розетки), марка ЭВ
- вывод В1 (код — в ведомости привязок)
- вывод Т3 (код — в ведомости привязок)
- вывод К1 (код — в ведомости привязок)
- привязки точек и выводов от угла и от пола, мм
- марка развёртки: буква стены, стрелка — взгляд

Схема развёрток (М 1:50)

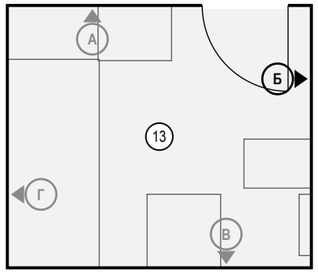

Допущения и предложения на листе

Основа листа: взаимное расположение помещений, контур дома 9600 × 8000 и раскладка этажей подобраны проектировщиком под габариты помещений брифа; обмер и проект АР — задание (К-1); высота потолка 2900 мм — по брифу, не замерена; перекрытие 330 мм и отметка 2-го этажа +3,230 приняты; проект КР — задание (К-2); наружные стены 400 мм, перегородки 120 мм приняты (в брифе толщин нет) (К-1); разрешённая мощность 15 кВт принята по типовым ТУ для частного дома (К-4); подрайон климата не задан — принят не северный (жилые от 2,5 м) (К-7).

Знак «*» — принято, не замерено и не подтверждено (замерить на объекте): К-1: дверь пом. 13 (стена А) — Петли у правого откоса (х 6150, у стояков): открытое полотно стоит вдоль стены Б, вошедший идёт влево к умывальнику и ванне; К-2: отметка чистого пола этажа «2-й этаж» +3,230 — отметка чистого пола 2-го этажа +3,230 принята: высота потолка 2900 по брифу + перекрытие с полом 330 (конструкция перекрытия не задана; проект КР — задание).

Знак «**» — предложение проектировщика, заказчиком не утверждено (согласовать с заказчиком): ЭВ4 — Вентилятор ВР1 на стене Б у потолка, offset 300 (над зоной входа); ИЗ-1: КУП1 — КУП за унитазом См2 (1150…1550) ниже — offset 1850, Н=300; ИЗ-1, ИЗ-2: ЭВ6 — Вывод полотенцесушителя См5 (стена Б, 1600…2100).

См. лист открытых вопросов (лист 7, записи К-1, К-2, К-4; лист 8, запись К-7; лист 9, записи ИЗ-1, ИЗ-2).

Примечания

1. Вид «Привязки» стены Б — электроточки и выводы ВК; архитектурная развёртка (мебель, отделка, проёмы, высоты) — на листе 164, расположение — на листе 117. Мебель и приборы — подложкой для ориентира; их марки и обозначения мебели, проёмов и стен — там же.
2. Привязки — в мм: по горизонтали от левого чистового угла стены до оси изделия, Н — от чистого пола до оси; все точки — в таблице привязок. Красная цепочка — привязки по осям; точки ближе 150 мм одна к другой в цепочку не дробятся — их привязки только в таблице.
3. У знака — марка электроточки (Р — розетка, S — выключатель, Св — светильник, ЭВ — вывод кабеля); посты в рамке и группа щита — в графе «Примечание»; группы по клавишам выключателя — на листе выключателей.
4. Коды выводов ВК: В1 — холодная вода, Т3 — горячая вода, К1 — канализация; номер после дефиса — номер вывода на листе выводов сантехники; * — высота принята по типовой практике монтажа, окончательно — по паспорту прибора.

1000 мм · печать 1:1

Изм.	Кол.уч	Лист	№ док.	Подп.	Дата
Разраб.		Кырлан А.С.			04.11.26
Пров.					
ГИП					
Н. контр.					
Утв.					

ГД-2026-012-АИ

Дом 120 м²

Общая площадь 147,36* м² · * размеры приняты, не замерены (реестр — л. 7–9, К-1)

Дизайн-проект интерьера

Стадия	Лист	Листов
РП	166	175

Привязки электроточек и выводов ВК, стена Б. Санузел второго этажа (пом. 13)

М 1:25

Кырлан Александр Сергеевич


выпуск 04.11.2026 № 4dfa962484 · стр. 170 из 180

Развёртки стен В, Г. Санузел второго этажа (пом. 13)

Санузел второго этажа (пом. 13) · вид изнутри помещения · размеры в мм, отметки в м от ±0,000 (чистый пол 1-го этажа)


ПРЕДВАРИТЕЛЬНО · не для производства работ · открыто пунктов: 11 (реестр — л. 7–9)

Развёртка стены В

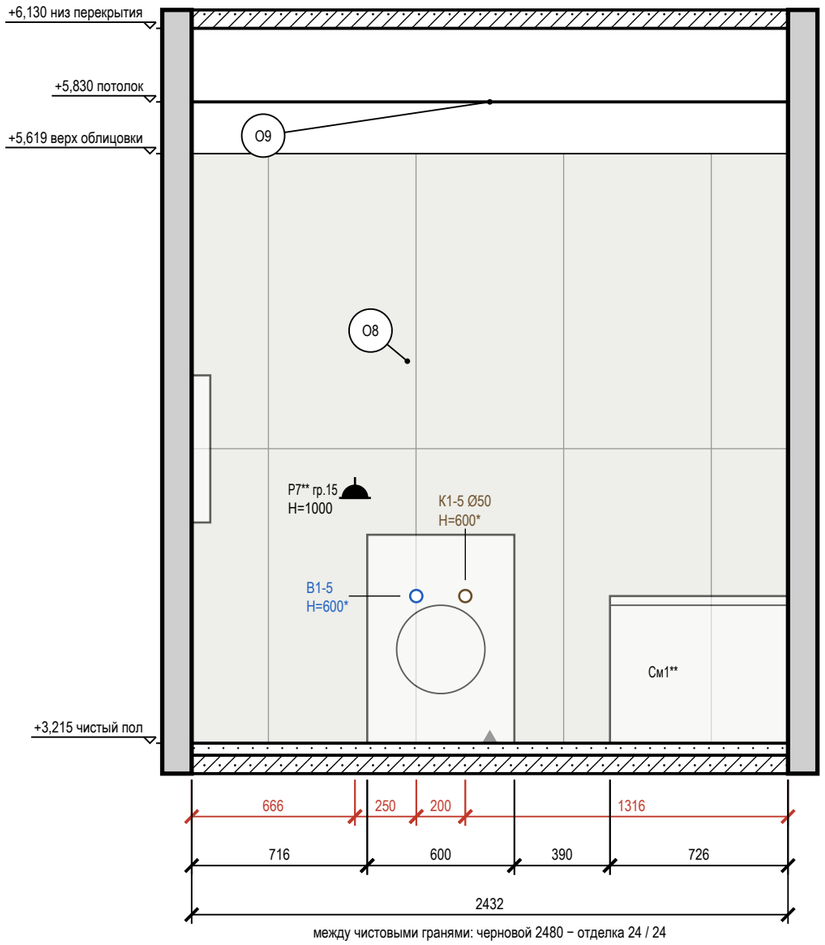

между чистовыми гранями: черновой 2480 − отделка 24 / 24

Развёртка стены Г

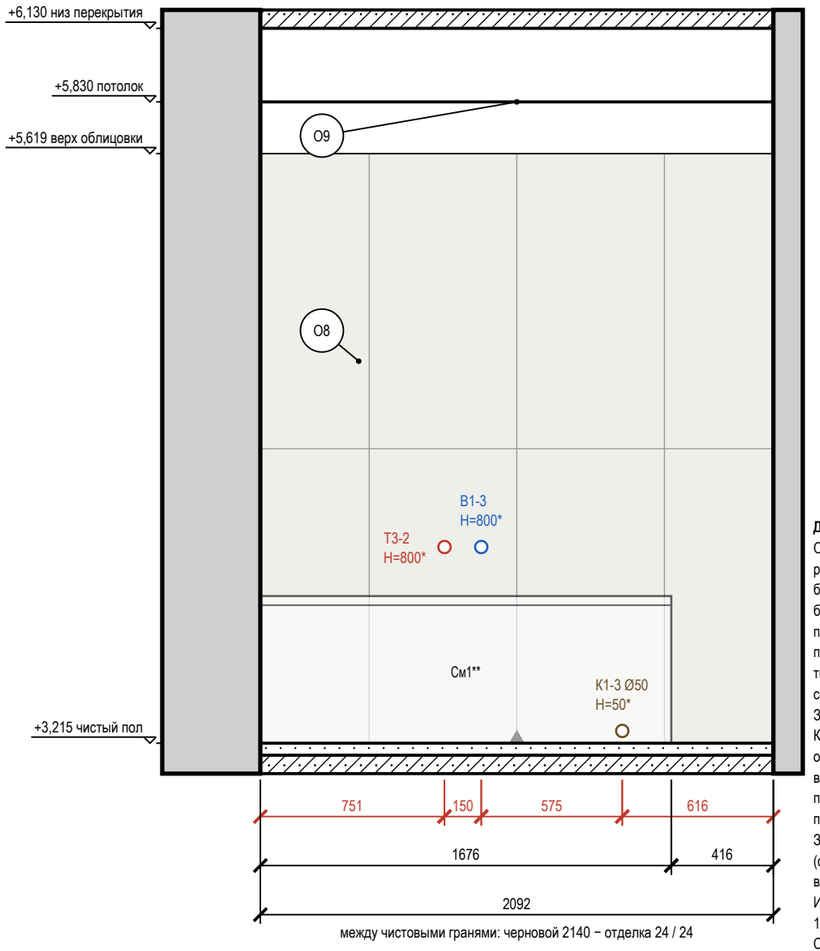

между чистовыми гранями: черновой 2140 − отделка 24 / 24

Условные обозначения

- розетка влагозащищённая IP44
- вывод В1 (код — в ведомости привязок)
- вывод Т3 (код — в ведомости привязок)
- вывод К1 (код — в ведомости привязок)
- привязки точек и выводов от угла и от пола, мм
- мебель и приборы — фасад по расстановке (условно)
- стены и перекрытия в сечении
- плитка: сетка швов по формату, ▲ — ось старта
- О1 — марка отделки по реестру отделки альбома
- А — марка развёртки: буква стены, стрелка — взгляд

Допущения и предложения на листе


Основа листа: взаимное расположение помещений, контур дома 9600 × 8000 и раскладка этажей подобраны проектировщиком под габариты помещений брифа; обмер и проект АР — задание (К-1); высота потолка 2900 мм — по брифу, не замерена; перекрытие 330 мм и отметка 2-го этажа +3,230 приняты; проект КР — задание (К-2); наружные стены 400 мм, перегородки 120 мм приняты (в брифе толщин нет) (К-1); разрешённая мощность 15 кВт принята по типовым ТУ для частного дома (К-4); подрайон климата не задан — принят не северный (жилые от 2,5 м) (К-7).

Знак «*» — принято, не замерено и не подтверждено (замерить на объекте): К-1: дверь пом. 13 (стена А) — Петли у правого откоса (х 6150, у стояков): открытое полотно стоит вдоль стены Б, вошедший идёт влево к умывальнику и ванне; К-2: отметка чистого пола этажа «2-й этаж» +3,230 — отметка чистого пола 2-го этажа +3,230 принята: высота потолка 2900 по брифу + перекрытие с полом 330 (конструкция перекрытия не задана; проект КР — задание).

Знак «**» — предложение проектировщика, заказчиком не утверждено (согласовать с заказчиком): ИЗ-1: См1 — Было у стены В offset 150 — заходила в полосу 600 мм перед проёмом Д-8 и в зону 750 перед машиной См3; ИЗ-1, ИЗ-2: Р7 — Розетка стиральной машины — за машиной См3 (стена В, 1200…1800), H=1000, вне зон 0–2 ванны (ванна у стены Г до х 4550).

См. лист открытых вопросов (лист 7, записи К-1, К-2, К-4; лист 8, запись К-7; лист 9, записи ИЗ-1, ИЗ-2).

Схема развёрток (М 1:100)

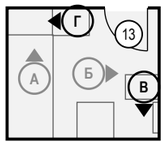

Ведомость отделки (на листе)

Марка	Поверхность	Материал, изделие	Цвет, код	Кол.
О8	стены	облицовка плиткой, Atlas Concorde Marvel Travertine, 600×1200×9 мм, A8UZ, затирка CG2WA	Atlas Concorde A8UZ «Marvel Travertine»	10,9 м²
О9	потолок	окраска, Little Greene Intelligent Bathroom, матовая, подготовка Q3	Little Greene No. 222 «Loft White»	5,3 м²

Примечания

1. Развёртки — вид на стену изнутри помещения, по часовой стрелке; расположение — на схеме листа и на листе 117; размеры — в мм по чистовым поверхностям; отметки — в м от ±0,000 (чистый пол 1-го этажа); высоты Н — от чистого пола помещения до оси изделия, у декора — до центра.
2. Красная цепочка — привязки электроточек и выводов по осям от угла чистовых стен; высота Н — у знака, от чистого пола до оси; высоты мебели, проёмов и границ отделки — колонкой отметок слева. Стена с 5 и более точками или с мелкими звеньями привязок показана двумя видами: архитектурная развёртка (мебель, отделка, проёмы, высоты) и вид «Привязки» на отдельном листе — точки и выводы с марками, одна цепочка по осям и таблица привязок (каждая точка — строка).
3. У знака электроточки: марка (Р — розетка, S — выключатель, Св — светильник, ЭВ — вывод кабеля), ×N — число постов в рамке, гр. — группа щита, Н — высота оси от чистого пола, мм; группы по клавишам выключателя — на листе выключателей.
4. Схема мебели, приборов и декора не является технической документацией для производства мебели; габариты — по паспортам изделий (* — высота не задана в проекте, показана по типовому изделию).
5. Выводы ВК — коды и высоты по листу выводов сантехники; * — высота принята по типовой практике монтажа, окончательно — по паспорту прибора.
6. Облицовка — по сетке швов 2 мм, раскладка от оси стены (треугольник у пола), целые ряды от пола; подрезки — по листу раскладки плитки.
7. Гидроизоляция в 2 слоя, заход на стены 200 мм; над ванной — до 2000 и 300 мм за борт — до облицовки, с актом скрытых работ и тестом проливом (узел — на листе узлов).

1000 мм · печать 1:1

Изм.	Кол.уч	Лист	№ док.	Подп.	Дата
Разраб.		Кырлан А.С.			04.11.26
Пров.					
ГИП					
Н. контр.					
Утв.					

ГД-2026-012-АИ

Дом 120 м²

Общая площадь 147,36* м² · * размеры приняты, не замерены (реестр — л. 7–9, К-1)

Дизайн-проект интерьера

Стадия	Лист	Листов
РП	167	175

Развёртки стен В, Г. Санузел второго этажа (пом. 13)

М 1:25

Кырлан Александр Сергеевич


выпуск 04.11.2026 № 4dfa962484 · стр. 171 из 180

Узлы

Пороги и стыки покрытий, скрытые двери, короба стояков, гидроизоляция, плинтус


1 Порог 15 мм: мокрая зона — смежное помещение (М 1:5)

Применение: двери Д-3, Д-8; места — листы 116, 117

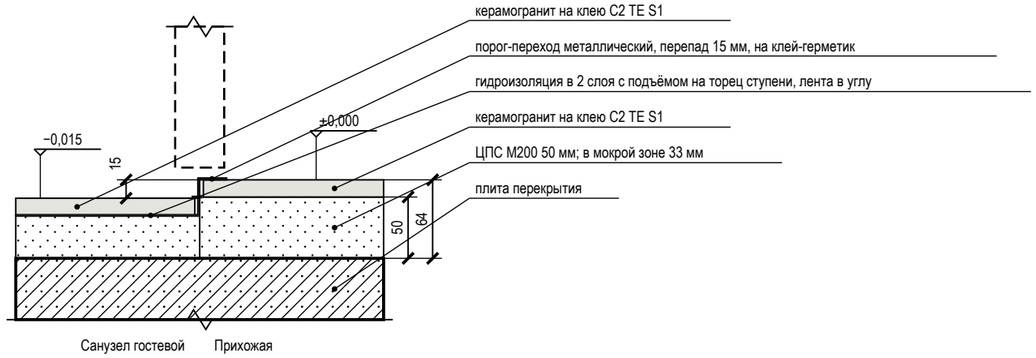

2 Дверь скрытого монтажа в плоскости стены, плинтус (М 1:5)


Применение: двери Д-1, Д-2, Д-3, Д-4, Д-5, Д-6, Д-7, Д-10, Д-9, Д-8; места — листы 116, 117

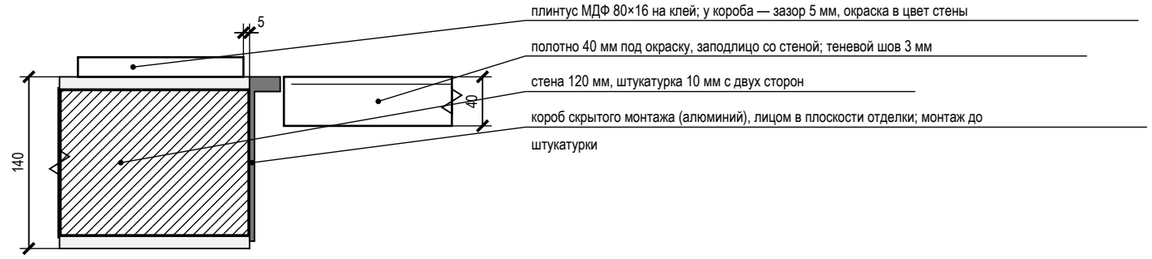

Допущения и предложения на листе. Основа листа: взаимное расположение помещений, контур дома 9600 × 8000 и раскладка этажей подобраны проектировщиком под габариты помещений брифа; обмер и проект АР — задание (К-1); высота потолка 2900 мм — по брифу, не замерена; перекрытие 330 мм и отметка 2-го этажа +3,230 приняты; проект КР — задание (К-2); наружные стены 400 мм, перегородки 120 мм приняты (в брифе толщин нет) (К-1); разрешённая мощность 15 кВт принята по типовым ТУ для частного дома (К-4); подрайон климата не задан — принят не северный (жилые от 2,5 м) (К-7). См. лист открытых вопросов (лист 7, записи К-1, К-2, К-4; лист 8, запись К-7).


3 Короб стояков К1-1 с люком и звукоизоляцией (М 1:10)

Применение: пом. 4, 1; места — лист 116

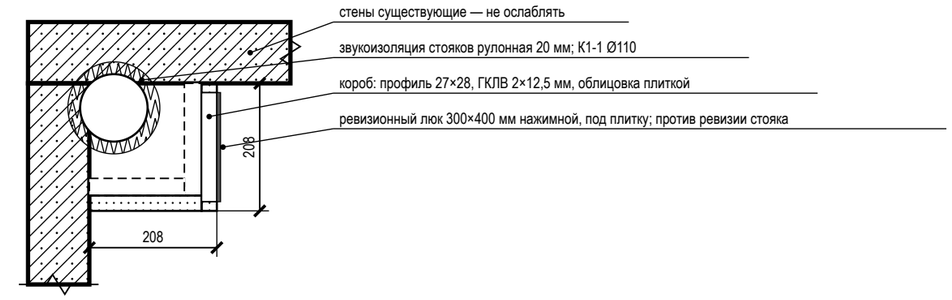


4 Гидроизоляция санузла: заход на стены 200 мм, примыкание ванны (М 1:20)

Применение: пом. 4, 13; места — листы 116, 117

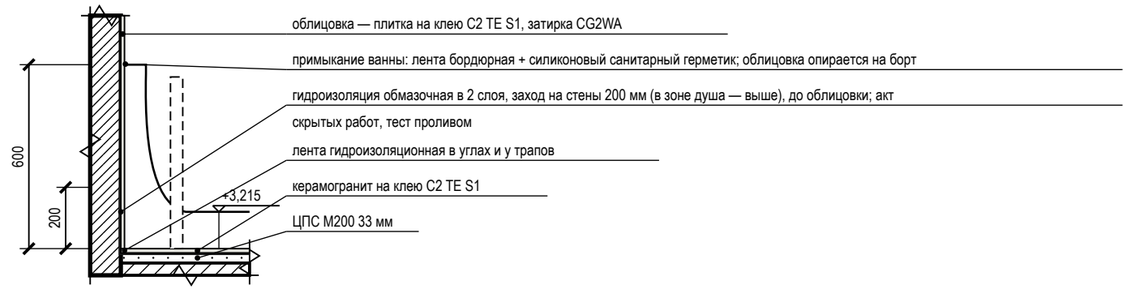


5 Плинтус МДФ 80×16 мм у окрашенной стены по доске (ламинату) (М 1:10)

Применение: пом. 1, 2, 3, 6, 7, 8, 9, 10, 11, 12; места — листы 116, 117

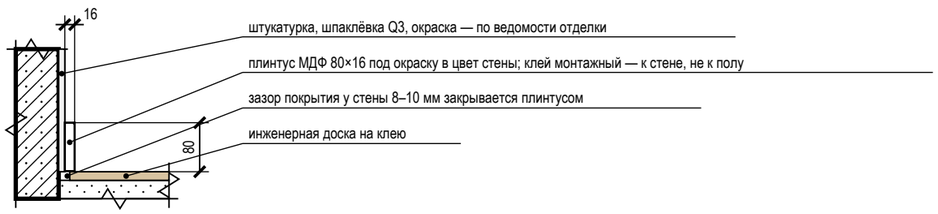

6 Плинтус МДФ 80×16 мм у окрашенной стены по керамограниту (плитке) (М 1:10)

Применение: пом. 5; места — лист 116

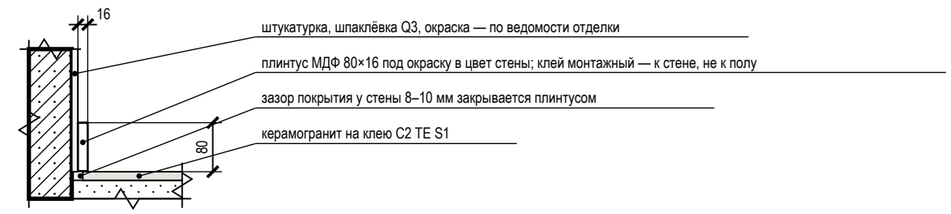

Условные обозначения

- железобетон (плита, стены) — условно: конструкция не установлена
- кладка, перегородка — условно: конструкция не установлена
- стяжка, раствор
- гипсокартон ГКЛВ
- звукоизоляция, эластичный заполнитель
- плитка, керамогранит на клею
- инженерная доска (покрытие пола)
- металлический профиль (порог, Т-профиль, короб двери)
- гидроизоляция (обмазочная, лента)

Примечания

1. Узлы — типовые решения проекта для мест, отмеченных выносками на листе схемы расположения развёрток и узлов; размеры — в мм, отметки — в м от ±0,000 (чистый пол 1-го этажа).
2. Узлы с гидроизоляцией, закладными и коробами скрытого монтажа принимаются по актам скрытых работ до закрытия отделкой; гидроизоляция — после теста проливом (24 ч).
3. Марки изделий (порог, Т-профиль, короб скрытой двери, люк) — по спецификациям; замена — на аналог с теми же габаритами по согласованию с автором проекта.
4. Материал плиты перекрытия и стен в узлах показан условно (железобетон, кладка): конструкция дома не установлена — крепёж, анкеры и толщины слоёв уточняются после обследования (до него — по допущениям общих указаний).
5. Узел 1 применяется на этажах: 1-й этаж, 2-й этаж; отметки показаны для пом. 5 (1-й этаж), на этаже «2-й этаж» — с поправкой +3,230 (разность отметок чистого пола этажей).
6. Узел 4 применяется на этажах: 1-й этаж, 2-й этаж; отметки показаны для пом. 13 (2-й этаж), на этаже «1-й этаж» — с поправкой −3,230 (разность отметок чистого пола этажей).

Изм.	Кол.уч	Лист	№ док.	Подп.	Дата
Разраб.		Кырлан А.С.			04.11.26
Пров.					
ГИП					
Н. контр.					
Утв.					

ГД-2026-012-АИ

Дом 120 м²

Общая площадь 147,36* м² · * размеры приняты, не замерены (реестр — л. 7–9, К-1)

Дизайн-проект интерьера

Стадия	Лист	Листов
РП	168	175

Узлы

М 1:5; 1:10; 1:20

Кырлан Александр Сергеевич

выпуск 04.11.2026 № 4dfa962484 · стр. 172 из 180

05

Смета

Кырлан Александр Сергеевич

выпуск 04.11.2026 · 4dfa962484 · стр. 173 из 180

Ведомость объёмов работ

ПРЕДВАРИТЕЛЬНО · не для производства работ · открыто пунктов: 11 (реестр — л. 7–9)

Объёмы по помещениям от чертежа · площади в м², длины в м · формула, правило проёмов и источник в каждой строке

Ведомость объёмов работ по помещениям

Поз.	Наименование работ (материал, число слоёв)	Ед. изм.	Объём по помещениям (№ по экспликации)													Всего	Формула подсчёта	Правило проёмов	Источник	Цена за ед., ₽	Стоимость, ₽
			1	2	3	4	5	6	7	8	9	10	11	12	13						
1. Демонтаж и черновые работы																					
1	Демонтаж существующего покрытия пола до основания	м²	31,32	15,51	11,00	4,17	12,20	17,17	12,30	3,82	4,66	15,51	5,16	9,23	5,31	147,36	S пом.		л. 17–20	по КП	
2	Демонтаж существующей отделки стен до основания	м²	52,21	33,04	33,48	19,15	40,60	39,77	34,11	22,06	23,61	33,04	17,94	29,12	21,01	399,14	P × H − проёмы	за вычетом проёмов	л. 17–20	по КП	
3	Демонтаж существующей отделки потолка до основания	м²	31,32	15,51	11,00	4,17	12,20	17,17	12,30	3,82	4,66	15,51	5,16	9,23	5,31	147,36	S пом.		л. 17–20	по КП	
4	Демонтаж существующих дверных блоков	шт	1		1	1	2	1	1	1	1			1	1	11	по ведомости проёмов		л. 19–23	по КП	
5	Демонтаж существующих сантехприборов и электрооборудования (если есть)	компл															по факту на объекте		л. 19, 20	по КП	
6	Устройство стяжки: стяжка ЦПС М200, 50 мм	м²	31,37	15,82	11,05	4,24	12,54	17,22	12,35	3,86	4,71	15,82	5,36	9,28	5,40	149,02	S пом. + S в дверных проёмах (b × t/2)	проёмы добавлены	л. 78–82	530	78 981
7	Гидроизоляция обмазочная, 2 слоя: пол, стены на 200 мм, зоны замачивания	м²				5,45									12,37	17,82	пол + (P − двери) × h заведения + зоны замачивания		л. 74	450	8 019
8	Штукатурка стен по маякам, до 10 мм	м²	52,21	33,04	33,48	19,15	40,60	39,77	34,11	22,06		33,04	17,94	29,12	21,01	375,53	P × H − проёмы по обводу коробок − грани перегородок на ГКЛВ	за вычетом проёмов	л. 17, 18, 80–82	530	199 031
9	Штукатурка оконных откосов шириной более 200 мм	м²	3,53	1,32	1,49			1,58	1,45			1,32		1,42		12,11	Σ (2h + b) × глубина откоса	откосы > 200 мм	л. 17, 18	540	6 539
10	Потолок ГКЛ по каркасу П113, 1 слой	м²	31,32	11,51	11,00	4,17	12,20	17,17	12,30			15,51	5,16	9,23	5,31	134,88	S пом. по плану потолков		л. 66–73	1 500	202 320
11	Балки декоративные 140×100 мм под потолком (фальш-балка, массив сосны, белёная (известковая морилка)): изделие и монтаж на закладные	м	8,10													8,10	3 шт. по плану потолков		л. 66–73	по КП	
Итого по разделу 1 — 494 890 ₽ (позиций 11, из них по КП 6); в сводную смету — л. 174, 175																					
2. Инженерные системы																					
12	Прокладка кабеля ВВГнг(A)-LS по группам щита: за потолком и в штробах стен (штробы — только после технического заключения, см. строку «Штробы в стенах»)	м														742,70	Σ длин групп щита		л. 42, 43	60	44 562
13	Прокладка слаботочной линии: Кабель домофона — тип по системе поставщика, отдельно от силовых	м														6,10	по лучам от ЩС**: 1 точ., запас 10 %		л. 46, 47	по КП	
14	Прокладка слаботочной линии: Кабель коаксиальный RG-6 (75 Ом) к розеткам ТВ, отдельно от силовых	м														16,70	по лучам от ЩС**: 1 точ., запас 10 %		л. 46, 47	по КП	
15	Прокладка слаботочной линии: Кабель U/UTP кат. 6 (LAN, Wi-Fi и камеры по PoE), отдельно от силовых	м														71,00	по лучам от ЩС**: 6 точ., запас 10 %		л. 46, 47	по КП	
16	Прокладка гофротрубы Ø20 для слаботочных линий, отдельно от силовых	м														84,40	по длине лучей без участков в канале плинтуса (≈ 90 %)		л. 46, 47	по КП	
17	Сборка слаботочного щита ЩС**: корпус, патч-панель, подключение линий и питания 220 В; коммутатор и точки доступа — оборудование заказчика	шт														1	один щит		л. 40, 41, 46, 47	по КП	
18	Электроточка: подрозетник в бетоне, розетка, выключатель, вывод	шт	24	3	7	3	8	9	7			3	3	7	4	78	по ведомости электроточек		л. 34, 35, 40, 41	950	74 100
19	Штробы в стенах под спуски кабеля к точкам — выполняются только после технического заключения о несущих стенах	м	43,00	6,30	16,30	3,54	12,75	17,75	15,40			6,30	6,15	15,40	5,36	148,25	Σ (H − h) по точкам на стенах: вертикальные спуски	после техзаключения	л. 19, 20, 34, 35	по КП	
20	Установка встраиваемого точечного светильника	шт	14	2	6	2	6	8	6			2	2	6	3	57	по плану освещения		л. 36, 37	750	42 750

Допущения и предложения на листе

Основа листа: взаимное расположение помещений, контур дома 9600 × 8000 и раскладка этажей подобраны проектировщиком под габариты помещений брифа; обмер и проект АР — задание (К-1); высота потолка 2900 мм — по брифу, не замерена; перекрытие 330 мм и отметка 2-го этажа +3,230 приняты; проект КР — задание (К-2); наружные стены 400 мм, перегородки 120 мм приняты (в брифе толщин нет) (К-1); разрешённая мощность 15 кВт принята по типовым ТУ для частного дома (К-4); подрайон климата не задан — принят не северный (жилые от 2,5 м) (К-7).

Знак «**» — предложение проектировщика, заказчиком не утверждено (согласовать с заказчиком): ИЗ-2: ЩС — щит слаботочный: место и состав.

См. лист открытых вопросов (лист 7, записи К-1, К-2, К-4; лист 8, запись К-7; лист 9, запись ИЗ-2).

Изм.	Кол.уч	Лист	№ док.	Подп.	Дата
Разраб.		Кырлан А.С.			04.11.26
Пров.					
ГИП					
Н. контр.					
Утв.					

ГД-2026-012-АИ

Дом 120 м²

Общая площадь 147,36* м² · * размеры приняты, не замерены (реестр — л. 7–9, К-1)

Дизайн-проект интерьера

Стадия	Лист	Листов
РП	169	175

Ведомость объёмов работ

М б/м

Кырлан Александр Сергеевич

Ведомость объёмов работ (продолжение)

Объёмы по помещениям от чертежа · площади в м², длины в м · формула, правило проёмов и источник в каждой строке

Ведомость объёмов работ по помещениям (продолжение)

Поз.	Наименование работ (материал, число слоёв)	Ед. изм.	Объём по помещениям (№ по экспликации)													Всего	Формула подсчёта	Правило проёмов	Источник	Цена за ед., ₽	Стоимость, ₽
			1	2	3	4	5	6	7	8	9	10	11	12	13						
21	Монтаж светильника: потолочного, подвесного, настенного	шт	3	1		1		2	1	1	1			1	1	12	по плану освещения		л. 36, 37	1 200	14 400
22	Монтаж LED-ленты в алюминиевый профиль	м	23,50		5,70		1,80	4,50	12,00					10,10		57,60	Σ длин лент по плану освещения		л. 36, 37	230	13 248
23	Установка блока питания LED в доступном месте (люк, шкаф)	шт	2		1		1	1	1					1		7	один на LED-группу		л. 36, 37	570	3 990
24	Установка автономного пожарного извещателя	шт	2	1	1		1	1	1			1	1	1		10	по плану розеток		л. 34, 35	по КП	
25	Сборка щита: установка автоматов и АВДТ групп, вводного автомата	шт														18	группы + вводной автомат		л. 42, 43	230	4 140
26	Установка вводного УЗО	шт														1	по однолинейной схеме		л. 42, 43	380	380
27	Монтаж инсталляции, установка подвесного унитаза и кнопки смыва	шт				1									1	2	по плану выводов		л. 52, 53, 63	10 500	21 000
28	Короб инсталляции: каркас и обшивка ГКЛВ в 2 слоя, ревизионный доступ к смыву	шт				1									1	2	по плану выводов		л. 52, 53, 74–77	по КП	
29	Короб К1 над чистым полом: каркас и обшивка ГКЛВ под плитку (материалы — в спецификации ВК)	м.п.				3,05									5,52	8,57	Σ открытых участков выпусков К1 (профиль листа разводки ВК)		л. 52, 53, 63	по КП	
30	Установка ванны с сифоном	шт													1	1	по плану выводов		л. 52, 53, 63	6 000	6 000
31	Установка умывальника (мойки) с сифоном и смесителем	шт				1									1	2	по плану выводов		л. 52, 53, 63	3 000	6 000
32	Подключение стиральной (посудомоечной) машины к ВК	шт													1	1	по плану выводов		л. 52, 53	по КП	
33	Установка радиатора с узлом подключения и терморегулятором	шт	1	1	1		1	1	1			1		1		8	по плану отопления		л. 50, 51	по КП	
Итого по разделу 2 — 230 570 ₽ (позиций 22, из них по КП 11); в сводную смету — л. 174, 175																					
3. Чистовые работы																					
34	Облицовка стен керамогранитом 600×1200 на клею	м²				16,68									18,10	34,78	по раскладке: зона облицовки − место за коробом	за вычетом проёмов	л. 74–77	2 500	86 950
35	Облицовка короба инсталляции (ГКЛВ) керамогранитом: лицо, боковины, полка	м²				1,47									1,76	3,23	по раскладке: лицо, боковины, полка		л. 74–77	2 500	8 075
36	Облицовка фартука керамогранитом 1200×600	м²	1,94													1,94	по раскладке фартука		л. 74–77, 80–82	2 400	4 656
37	Укладка керамогранита на пол, 600×600, на клею	м²				4,24	12,54								5,40	22,18	S пом. + S в дверных проёмах	проёмы добавлены	л. 74–79	1 800	39 924
38	Затирка швов керамогранита	м²	1,94			22,32	12,20								25,17	61,63	Σ S облицовки и пола из плитки		л. 74–77	150	9 245
39	Грунтование стен, 2 слоя (под штукатурку и под отделку)	м²	52,21	33,04	33,48	19,15	40,60	39,77	34,11	22,06	23,61	33,04	17,94	29,12	21,01	399,14	P × H − проёмы	за вычетом проёмов	л. 80–82	96	38 317
40	Шпаклёвка стен под окраску, 2 слоя (старт и финиш), уровень Q3	м²	50,27	33,04	33,48		40,60	39,77	34,11	22,06	23,61	33,04	17,94	29,12		357,04	P × H − проёмы − фартук	за вычетом проёмов	л. 80–82	750	267 780
41	Грунтование и шпаклёвка оконных откосов, 2 слоя	м.п.	10,70	4,00	4,50			4,80	4,40			4,00		4,30		36,70	Σ (2h + b) по окнам	по окнам	л. 17, 18	300	11 010
42	Грунтование потолка, 2 слоя	м²	31,32	15,51	11,00	4,17	12,20	17,17	12,30	3,82	4,66	15,51	5,16	9,23	5,31	147,36	S пом.		л. 80–82	96	14 147
43	Шпаклёвка потолка под окраску, 2 слоя, уровень Q3	м²	31,32	15,51	11,00	4,17	12,20	17,17	12,30	3,82	4,66	15,51	5,16	9,23	5,31	147,36	S пом.		л. 66–73, 80–82	950	139 992
44	Окраска потолка водно-дисперсионной краской, 2 слоя	м²	31,32	15,51	11,00	4,17	12,20	17,17	12,30	3,82	4,66	15,51	5,16	9,23	5,31	147,36	S пом.		л. 80–82	360	53 050
45	Окраска стен водно-дисперсионной краской, 2 слоя	м²	58,97	45,25	37,41		47,74	44,15	37,96	23,32	25,29	45,25	25,08	32,83		423,25	P × H − фартук, проёмы не вычитаются	без вычета проёмов	л. 80–82	300	126 975
46	Окраска оконных откосов, 2 слоя	м.п.	10,70	4,00	4,50			4,80	4,40			4,00		4,30		36,70	Σ (2h + b) по окнам	по окнам	л. 17, 18	120	4 404

Допущения и предложения на листе

Основа листа: взаимное расположение помещений, контур дома 9600 × 8000 и раскладка этажей подобраны проектировщиком под габариты помещений брифа; обмер и проект АР — задание (К-1); высота потолка 2900 мм — по брифу, не замерена; перекрытие 330 мм и отметка 2-го этажа +3,230 приняты; проект КР — задание (К-2); наружные стены 400 мм, перегородки 120 мм приняты (в брифе толщин нет) (К-1); разрешённая мощность 15 кВт принята по типовым ТУ для частного дома (К-4); подрайон климата не задан — принят не северный (жилые от 2,5 м) (К-7).

См. лист открытых вопросов (лист 7, записи К-1, К-2, К-4; лист 8, запись К-7).

Изм.	Кол.уч	Лист	№ док.	Подп.	Дата
Разраб.		Кырлан А.С.			04.11.26
Пров.					
ГИП					
Н. контр.					
Утв.					

ГД-2026-012-АИ

Дом 120 м²

Общая площадь 147,36* м² · * размеры приняты, не замерены (реестр — л. 7–9, К-1)

Дизайн-проект интерьера

Стадия	Лист	Листов
РП	170	175

Ведомость объёмов работ (продолжение)

М б/м

Кырлан Александр Сергеевич

Ведомость объёмов работ (окончание)

Объёмы по помещениям от чертежа · площади в м², длины в м · формула, правило проёмов и источник в каждой строке

Ведомость объёмов работ по помещениям (продолжение)

Поз.	Наименование работ (материал, число слоёв)	Ед. изм.	Объём по помещениям (№ по экспликации)													Всего	Формула подсчёта	Правило проёмов	Источник	Цена за ед., ₽	Стоимость, ₽
			1	2	3	4	5	6	7	8	9	10	11	12	13						
47	Укладка инженерной доски на клей	м²	31,37	15,82	11,05			17,22	12,35	3,86	4,71	15,82	5,36	9,28		126,84	S пом. + S в дверных проёмах	проёмы добавлены	л. 78–82	1 200	152 208
48	Установка плинтуса МДФ h=80 мм	м.п.	21,66	11,06	12,56		13,96	15,86	13,26	7,44	7,92	11,06	5,72	11,36		131,86	P − ширина дверных проёмов		л. 80–82	450	59 337
49	Окраска плинтуса в тоне G503, 2 слоя	м.п.	21,66	11,06	12,56		13,96	15,86	13,26	7,44	7,92	11,06	5,72	11,36		131,86	как плинтус		л. 80–82	300	39 558
50	Монтаж дверей скрытого монтажа под покраску (поставщик дверей)	шт	1		1	1	1	1	1	1	1			1	1	10	по ведомости проёмов		л. 21–23	5 250	52 500
51	Входная дверь, поставка с монтажом и откосами	шт														1	по ведомости проёмов		л. 21–23	по КП	
Итого по разделу 3 — 1 108 128 ₽ (позиций 18, из них по КП 1); в сводную смету — л. 174, 175																					

Ведомость подсчёта площадей по помещениям

№	Помещение	S пола, м²	P, м	H, м	P × H, м²	Проёмы, м²	Стены нетто, м²	В дверных проёмах, м²	Плинтус, м	Откосы, м.п.
1	Гостиная-кухня	31,32	22,56	2,70	60,91	8,70	52,21	0,05	21,66	10,70
2	Холл с лестницей	15,51	16,16	2,80	45,25	12,21	33,04	0,31	11,06	4,00
3	Кабинет	11,00	13,36	2,80	37,41	3,93	33,48	0,05	12,56	4,50
4	Санузел гостевой	4,17	8,32	2,62	21,76	2,60	19,15	0,07	нет	нет
5	Прихожая	12,20	17,36	2,75	47,74	7,14	40,60	0,34	13,96	нет
6	Спальня родителей	17,17	16,66	2,65	44,15	4,38	39,77	0,05	15,86	4,80
7	Детская	12,30	14,06	2,70	37,96	3,85	34,11	0,05	13,26	4,40
8	Гардеробная	3,82	8,04	2,90	23,32	1,26	22,06	0,04	7,44	нет
9	Кладовая	4,66	8,72	2,90	25,29	1,68	23,61	0,05	7,92	нет
10	Холл второго этажа	15,51	16,16	2,80	45,25	12,21	33,04	0,31	11,06	4,00
11	Коридор второго этажа	5,16	9,12	2,75	25,08	7,14	17,94	0,20	5,72	нет
12	Детская вторая	9,23	12,16	2,70	32,83	3,71	29,12	0,05	11,36	4,30
13	Санузел второго этажа	5,31	9,24	2,62	24,16	3,15	21,01	0,09	нет	нет
	Итого	**147,36**			**471,10**	**71,97**	**399,13**	**1,65**	**131,86**	**36,70**

Реестр контрольных сумм

Показатель	По ВОР	По чертежу	Расхождение	Лист
Σ площадей помещений без летних, м² — общая площадь по экспликации	147,36	147,36	0,0 %	л. 17, 18
Стены под окраску, м² (шпаклёвка) ведомость отделки	357,04	357,03	0,0 %	л. 80–82
Потолки под окраску, м² — ведомость отделки	147,36	147,36	0,0 %	л. 80–82
Плинтус, м — ведомость отделки	131,86	131,86	0,0 %	л. 80–82
Плитка к заказу, шт — ведомость плитки	164	164	0,0 %	л. 74
Гидроизоляция, м² — ведомость материалов плитки	17,82	17,82	0,0 %	л. 74
Точки ЭОМ, шт — планы ЭОМ (без щитов)	171	173	-1,2 %	л. 34–37

Примечания

1. Объёмы — от геометрии проекта (та же, что на планах и в ведомости отделки), не от общей площади: P — периметр чистого контура, H — от чистого пола до низа потолка, проёмы — по наружному обводу коробок.
2. Подсчёт по ГЭСН-2001-15 и ГЭСН-2001-11: штукатурка и шпаклёвка стен — за вычетом проёмов; окраска водными составами — без вычета проёмов (п. 2.24); откосы — отдельно, по ширине до 200 и более 200 мм; полы — с площадью в дверных проёмах.
3. Плитка — по раскладке (целые и с подрезкой); короб инсталляции и фартук — отдельными строками, двойного счёта облицовки нет. Материалы, запас и количество к заказу — в спецификации материалов.
4. Цены — ориентир по открытым прайсам Москвы (цены на 21.09.2026), не коммерческое предложение; «по КП» — расценки нет, строка в итог не входит.
5. Демонтаж — по плану демонтажа и общим указаниям: покрытия пола, отделка стен и потолков, дверные блоки — до основания; объёмы справочные — по плану демонтажа (расценки в книге нет — «по КП»).
6. Штробы в стенах — только после технического заключения о несущих стенах (общие указания, план обмера и демонтажа): строка «Штробы в стенах» вертикальные спуски кабеля от потолочной трассы к точкам, объём не меньше фактического (горизонтальные трассы — по исполнительной схеме). Расценки штробления в прайсе нет — «по КП», в итог не входит; кабель в штробах стен прокладывается после неё.
7. Площадь облицовки стен — одно число с тремя названиями: зона облицовки по ведомости отделки 36,46 м² − место за коробом инсталляции 1,68 м² (плитку туда не кладут) = стены под плитку 34,78 м² (строка «Облицовка стен»); облицовка коробов 3,23 м² — отдельной строкой; стены и короба вместе — 38,01 м² (столько плитки по раскладке в спецификации). Источник — один (quantities.js), расхождение на листах ловит.
8. Слаботочные сети: кабель по лучам от ЩС** 93,80 м (U/UTP, RG-6, домофон — по видам), гофра 84,40 м, щит ЩС** с патч-панелью; розетки RJ45 и ТВ монтируются в строке «Электроточка». Длины те же, что в ведомости изделий электрика (одна модель — lowcurrent-engineer/bom.js); оборудование заказчика (точки доступа, камеры, коммутатор) в спецификацию не входит. 2 точ. — предложение листа слаботочки.
9. Коробы: стояков (нет) и К1 над чистым полом (8,57 м открытых участков; труба К1 вдоль стен 17,64 м в короб не зашивается — она за приборами, в раме инсталляции и в шахтах). В спецификации ВК короб К1 заказывается с запасом 10 % — 9,50 м. Материалы коробов стояков и инсталляции — в спецификации материалов, К1 — в спецификации ВК.

Допущения и предложения на листе

Основа листа: взаимное расположение помещений, контур дома 9600 × 8000 и раскладка этажей подобраны проектировщиком под габариты помещений брифа; обмер и проект АР — задание (К-1); высота потолка 2900 мм — по брифу, не замерена; перекрытие 330 мм и отметка 2-го этажа +3,230 приняты; проект КР — задание (К-2); наружные стены 400 мм, перегородки 120 мм приняты (в брифе толщин нет) (К-1); разрешённая мощность 15 кВт принята по типовым ТУ для частного дома (К-4); подрайон климата не задан — принят не северный (жилые от 2,5 м) (К-7).
Знак «**» — предложение проектировщика, заказчиком не утверждено (согласовать с заказчиком): ИЗ-2: ЩС — щит слаботочный: место и состав.
См. лист открытых вопросов (лист 7, записи К-1, К-2, К-4; лист 8, запись К-7; лист 9, запись ИЗ-2).

Изм.	Кол.уч	Лист	№ док.	Подп.	Дата				
Разраб.		Кырлан А.С.			04.11.26	**ГД-2026-012-АИ**			
Пров.						Дом 120 м²			
ГИП						Общая площадь 147,36* м² · * размеры приняты, не замерены (реестр — л. 7–9, К-1)			
						Дизайн-проект интерьера	Стадия	Лист	Листов
Н. контр.							РП	171	175
Утв.						**Ведомость объёмов работ (окончание)** М б/м	**Кырлан Александр Сергеевич**		

Спецификация материалов

Отделочные материалы: чистое количество, запас, упаковка, к заказу · ГОСТ 21.110-2013

ПРЕДВАРИТЕЛЬНО · не для производства работ · открыто пунктов: 11 (реестр — л. 7–9)

Спецификация материалов (ГОСТ 21.110-2013, форма 1)

Поз.	Наименование и техническая характеристика	Тип, марка, артикул	Код продукции	Поставщик	Ед. изм.	Количество				Масса ед., кг	Примечание
						чистое	запас, %	упаковка	к заказу		
Покрытия полов и облицовка											
1	Инженерная доска (дуб натуральный, рабочий слой 4 мм, эмиссия E1, прямая укладка)	1167-4250			м²	126,83	7	по артикулу	135,80 м²		пом. 1, 2, 3, 6, 7, 8, 9, 10, 11, 12; до целой упаковки; л. 78–82
2	Клей для паркетной и инженерной доски (эластичный, по ТУ изготовителя доски)	по выбору подрядчика			м²	126,83		ведро по ТУ	по ТУ		расход кг/м² — по ТУ клея; л. 78, 79
3	Керамогранит 600×600 мм под травертин	аналог: керамогранит под травертин			шт	35	10	коробка	39 шт		9 целых + 26 с подрезкой; 9,48 м² по раскладке, к заказу 14,04 м²; пом. 4, 13; л. 74–77
4	Керамогранит 600×1200 мм A8UZ	A8UZ			шт	103	10	коробка	116 шт		32 целых + 71 с подрезкой; 50,21 м² по раскладке, к заказу 83,52 м²; пом. 4, 5, 13; л. 74–77
5	Керамогранит 1200×600 мм под травертин, матовый	аналог: керамогранит под травертин, матовый			шт	7	10	коробка	9 шт		0 целых + 7 с подрезкой; 1,94 м² по раскладке, к заказу 6,48 м²; пом. 1; л. 74–77
Сухие смеси и гидроизоляция											
6	Клей плиточный цементный класса C2 TE S1 (ГОСТ Р 56387-2018)	Ceresit CM 17 или аналог			кг	468,66	10	мешок 25 кг	21 меш.	25	слой 5 мм, 1,50 кг/м² на 1 мм; л. 74
7	Затирка цементная класса CG2WA, цвет — по колерной карте	Mapei Ultracolor Plus 132 или аналог			кг	4,71	10	упак. 2 кг	3 упак.	2	расход (a+b)/ab × шов × t × 1,6 кг/м²; л. 74
8	Гидроизоляция обмазочная полимерная, 2 слоя, лента в углах, манжеты на выводах	по выбору подрядчика			м²	17,82	10	ведро по ТУ	по ТУ		пом. 4, 13; расход кг/м² — по ТУ; л. 74
9	Лента демпферная по периметру пола из плитки	по выбору подрядчика			м	30,32	10	рулон	34,00 м		л. 74
10	Смесь цементно-песчаная для стяжки М200 (50 мм, 33 мм)	по выбору подрядчика			м³	7,29	5	мешок по ТУ	по ТУ		S 149,02 м² × толщина; армирование и маяки — по ТУ; л. 78, 79
11	Смесь штукатурная гипсовая для машинного и ручного нанесения по маякам, слой до 10 мм	по выбору подрядчика			м²	375,53	10	мешок по ТУ	по ТУ		пом. 1, 2, 3, 4, 5, 6, 7, 8, 10, 11, 12, 13; расход кг/м² на 1 мм слоя по ТУ смеси, толщина — по замеру кривизны стен; л. 17, 18, 80–82
Короба из ГКЛВ											
12	Лист ГКЛВ 12,5 мм, 2500 × 1200 мм, обшивка коробов в 2 слоя	по выбору подрядчика			м²	6,46	10	лист 3,00 м²	3,00 лист		инсталляция пом. 4: 1,47 м²; инсталляция пом. 13: 1,76 м²; площадь × 2 слоя; короб К1 над полом — в спецификации ВК; л. 52, 53, 74–77
13	Профиль стальной оцинкованный 27 × 28 мм: каркас коробов (стойки и направляющие)	по выбору подрядчика			м	15,60	10	хлыст 3 м	6 шт		стойки через 400 мм по свободному периметру + направляющие по полу и потолку; крепёж, лента, шпаклёвка швов — по узлу короба; л. 52, 53, 74–77
Слаботочные сети											
14	Кабель домофона — тип по системе поставщика	по выбору подрядчика			м	6,10		бухта по ТУ	7,00 м		по лучам от ЩС**, 1 точ., запас 10 % уже в длине; 2 точ. — предложение листа слаботочки (знак «*» на плане); л. 46, 47
15	Кабель коаксиальный RG-6 (75 Ом) к розеткам ТВ	по выбору подрядчика			м	16,70		бухта по ТУ	17,00 м		по лучам от ЩС**, 1 точ., запас 10 % уже в длине; 2 точ. — предложение листа слаботочки (знак «*» на плане); л. 46, 47
16	Кабель U/UTP кат. 6 (LAN, Wi-Fi и камеры по PoE)	по выбору подрядчика			м	71,00		бухта по ТУ	71,00 м		по лучам от ЩС**, 6 точ., запас 10 % уже в длине; 2 точ. — предложение листа слаботочки (знак «*» на плане); л. 46, 47
17	Гофротруба Ø20 для слаботочных линий, отдельно от силовых	по выбору подрядчика			м	84,40		бухта по ТУ	85,00 м		по длине лучей без участков в канале плинтуса (≈ 90 %); л. 46, 47
18	Розетка компьютерная RJ45, кат. 6, с рамкой и подрозетником	по выбору подрядчика			шт	4		шт	4 шт		LAN2–LAN5; серия механизмов — как у розеток и выключателей; л. 40, 41, 46, 47
19	Розетка телевизионная (коаксиальная) с рамкой и подрозетником	по выбору подрядчика			шт	1		шт	1 шт		ТВ1; серия механизмов — как у розеток и выключателей; л. 40, 41, 46, 47
20	Трубка или монитор домофона (поставка домофонной организации)	по выбору подрядчика			шт	1		шт	1 шт		ДФ1; серия механизмов — как у розеток и выключателей; л. 40, 41, 46, 47
21	Щит слаботочный ЩС**: корпус, DIN-рейка, розетки 220 В	по выбору подрядчика			шт	1		шт	1 шт		ЩС**; серия механизмов — как у розеток и выключателей; л. 40, 41, 46, 47

Допущения и предложения на листе

Основа листа: взаимное расположение помещений, контур дома 9600 × 8000 и раскладка этажей подобраны проектировщиком под габариты помещений брифа; обмер и проект АР — задание (К-1); высота потолка 2900 мм — по брифу, не замерена; перекрытие 330 мм и отметка 2-го этажа +3,230 приняты; проект КР — задание (К-2); наружные стены 400 мм, перегородки 120 мм приняты (в брифе толщин нет) (К-1); разрешённая мощность 15 кВт принята по типовым ТУ для частного дома (К-4); подрайон климата не задан — принят не северный (жилые от 2,5 м) (К-7).

Знак «**» — предложение проектировщика, заказчиком не утверждено (согласовать с заказчиком): плинтус пом. 1–3, 5, 6, 8, 10, 11, фартук пом. 1 — артикул изделия не выбран: позиция описана характеристиками («аналог по характеристикам»), артикул выбирается при закупке; пол пом. 4, 13 — пирог пола: стяжка 33 мм и обмазочная гидроизоляция добавлены разработчиком проекта; артикул изделия не выбран: позиция описана характеристиками («аналог по характеристикам»), артикул выбирается при закупке; ИЗ-2: ЩС — щит слаботочный: место и состав.

См. лист открытых вопросов (лист 7, записи К-1, К-2, К-4; лист 8, запись К-7; лист 9, запись ИЗ-2).

Изм.	Кол.уч	Лист	№ док.	Подп.	Дата
Разраб.		Кырлан А.С.			04.11.26
Пров.					
ГИП					
Н. контр.					
Утв.					

ГД-2026-012-АИ

Дом 120 м²

Общая площадь 147,36* м² · * размеры приняты, не замерены (реестр — л. 7–9, К-1)

Дизайн-проект интерьера	Стадия	Лист	Листов
	РП	172	175

Спецификация материалов

М б/м

Кырлан Александр Сергеевич

Спецификация материалов (окончание)

Отделочные материалы: чистое количество, запас, упаковка, к заказу · ГОСТ 21.110-2013

Спецификация материалов (ГОСТ 21.110-2013, форма 1) (продолжение)

Поз.	Наименование и техническая характеристика	Тип, марка, артикул	Код продукции	Поставщик	Ед. изм.	Количество				Масса ед., кг	Примечание
						чистое	запас, %	упаковка	к заказу		
22	Патч-панель, портов не менее 6	по выбору подрядчика			шт	1		шт	1 шт		серия механизмов — как у розеток и выключателей; л. 40, 41, 46, 47
Лакокрасочные материалы											
23	Краска интерьерная акриловая, матовая, класс истирания 1	Tikkurila S 3050-R80B «Эгейский синий»			л	2,47	10	банка 2,7 л	2 банк		10,31 м² × 2 сл. × 0,12 л/м²; пом. 1; л. 80–82
24	Краска интерьерная акриловая, матовая, класс истирания 1	Tikkurila G503 «Calla»			л	52,83	10	банка 2,7 л	22 банк		220,14 м² × 2 сл. × 0,12 л/м²; пом. 1, 2, 3, 5, 6, 10, 11; л. 80–82
25	Краска интерьерная акриловая, глубокоматовая, класс истирания 2	Little Greene Absolute Matt No. 222 «Loft White»			л	31,97	10	фасовка по артикулу	35,20 л		133,22 м² × 2 сл. × 0,12 л/м²; пом. 1 (пот.), 2 (пот.), 3 (пот.), 5 (пот.), 6 (пот.), 7 (пот.), 8 (пот.), 10 (пот.), 11 (пот.), 12 (пот.); л. 80–82
26	Краска интерьерная акриловая, матовая, класс истирания 1	Tikkurila S 5020-G90Y «Олива»			л	2,51	10	банка 2,7 л	2 банк		10,47 м² × 2 сл. × 0,12 л/м²; пом. 3; л. 80–82
27	Краска интерьерная акриловая, матовая, класс истирания 1	Little Greene Intelligent Bathroom No. 222 «Loft White»			л	2,28	10	фасовка по артикулу	2,60 л		9,48 м² × 2 сл. × 0,12 л/м²; пом. 4 (пот.), 13 (пот.); л. 80–82
28	Краска интерьерная акриловая, матовая, класс истирания 1	Farrow & Ball Modern Emulsion No. 89 «Lulworth Blue — светлая морская лазурь»			л	1,73	10	банка 2,5 л	1 банк		7,21 м² × 2 сл. × 0,12 л/м²; пом. 6; л. 80–82
29	Краска интерьерная акриловая, полуматовая, класс истирания 1	Farrow & Ball No. 66 «India Yellow — охра / горчица итальянских фасадов»			л	2,42	10	банка 2,5 л	2 банк		10,10 м² × 2 сл. × 0,12 л/м²; пом. 7; л. 80–82
30	Краска интерьерная акриловая, полуматовая, класс истирания 1	Tikkurila G503 «Calla»			л	11,12	10	банка 2,7 л	5 банк		46,33 м² × 2 сл. × 0,12 л/м²; пом. 7, 12; л. 80–82
31	Краска интерьерная акриловая, матовая, класс истирания 1	Little Greene Intelligent Matt No. 222 «Loft White»			л	5,29	10	фасовка по артикулу	5,90 л		22,06 м² × 2 сл. × 0,12 л/м²; пом. 8; л. 80–82
32	Краска интерьерная акриловая, матовая, класс истирания 2	Tikkurila S 0502-Y			л	5,67	10	банка 2,7 л	3 банк		23,61 м² × 2 сл. × 0,12 л/м²; пом. 9; л. 80–82
33	Краска интерьерная водно-дисперсионная, глубокоматовая, класс истирания 2	Tikkurila S 0300-N			л	1,12	10	банка 2,7 л	1 банк		4,66 м² × 2 сл. × 0,12 л/м²; пом. 9 (пот.); л. 80–82
34	Краска интерьерная акриловая, полуматовая, класс истирания 1	Tikkurila H440 «H440 Wave — бирюзово-голубая вода»			л	1,63	10	банка 2,7 л	1 банк		6,80 м² × 2 сл. × 0,12 л/м²; пом. 12; л. 80–82
35	Шпаклёвка финишная полимерная под окраску (стены и потолки, Q3)	по выбору подрядчика			м²	504,40	10	ведро по ТУ	по ТУ		расход кг/м² на слой — по ТУ; л. 80–82
36	Грунтовка акриловая глубокого проникновения, 2 слоя	по выбору подрядчика			м²	546,50	10	канистра по ТУ	по ТУ		расход л/м² — по ТУ; л. 80–82
Погонажные изделия и потолки											
37	Плинтус напольный МДФ под покраску, h=80 мм, крепление к стене	аналог: плинтус МДФ под покраску 80×16			м.п.	99,32	10	хлыст 2,4 м	46 шт		пом. 1, 2, 3, 5, 6, 8, 10, 11; длина хлыста — по артикулу; л. 80–82
38	Плинтус напольный МДФ под покраску, h=69 мм, крепление к стене	SX165			м.п.	32,54	10	хлыст 2,4 м	15 шт		пом. 7, 9, 12; длина хлыста — по артикулу; л. 80–82
39	Потолок подвесной ГКЛ/ГКЛВ по каркасу Knauf П113: листы, профили, подвесы, лента, шпаклёвка швов	Knauf П113			м²	134,88		комплект	по л. потолков		площадь — по ведомости потолков; число листов, профилей и подвесов — по шагам каркаса на листе потолков; л. 66–73

Примечания

1. Чистое количество — из ведомости объёмов работ и раскладки плитки; запас — отдельной графой (доска — по ведомости отделки, плитка, краска и плинтус — 10 %); «к заказу» — с запасом и кратно упаковке.
2. Плитка — штуками по раскладке, запас на каждую поверхность. Калибр (рабочий размер) и тон — одной партией на помещение, калибр указать при заказе и сверить с раскладкой до укладки.
3. Краска — 0,12 л/м² на слой (середина вилки 0,10–0,15 л/м²) по фактической площади окраски из ведомости отделки; колеровка одной партией.
4. «По ТУ» — расход задаёт производитель выбранного продукта; количество к заказу — после выбора марки.
5. Поз. 3, 5, 37 заданы характеристиками («аналог:»): марку, артикул и поставщика согласовать с заказчиком до закупки, без артикула не заказывать.
6. Штукатурная смесь — на ту же площадь, что строка ВОР «Штукатурка стен» (375,53 м²): площадь одна, расход смеси задаёт производитель.
7. Коробы инсталляции и стояков: ГКЛВ в 2 слоя и профиль 27 × 28 мм считаются по свободным граням коробов (источник — раскладка плиточника и шахты в данных); короб К1 над полом — в спецификации ВК.
8. Потолки ГКЛ: в этой спецификации — площадь системы П113; число листов, профилей и подвесов — по шагам каркаса на листе потолков (подвесы через 1000, несущие через 500, основные через 1200 мм), схема каркаса не выпущена. Сантехника, светильники и мебель — по своим спецификациям.

Допущения и предложения на листе

Основа листа: взаимное расположение помещений, контур дома 9600 × 8000 и раскладка этажей подобраны проектировщиком под габариты помещений брифа; обмер и проект АР — задание (К-1); высота потолка 2900 мм — по брифу, не замерена; перекрытие 330 мм и отметка 2-го этажа +3,230 приняты; проект КР — задание (К-2); наружные стены 400 мм, перегородки 120 мм приняты (в брифе толщин нет) (К-1); разрешённая мощность 15 кВт принята по типовым ТУ для частного дома (К-4); подрайон климата не задан — принят не северный (жилые от 2,5 м) (К-7).

Знак «**» — предложение проектировщика, заказчиком не утверждено (согласовать с заказчиком): плинтус пом. 1–3, 5, 6, 8, 10, 11, фартук пом. 1 — артикул изделия не выбран: позиция описана характеристиками («аналог по характеристикам»), артикул выбирается при закупке; пол пом. 4, 13 — пирог пола: стяжка 33 мм и обмазочная гидроизоляция добавлены разработчиком проекта; артикул изделия не выбран: позиция описана характеристиками («аналог по характеристикам»), артикул выбирается при закупке.

См. лист открытых вопросов (лист 7, записи К-1, К-2, К-4; лист 8, запись К-7).

Изм.	Кол.уч	Лист	№ док.	Подп.	Дата
Разраб.		Кырлан А.С.			04.11.26
Пров.					
ГИП					
Н. контр.					
Утв.					

ГД-2026-012-АИ

Дом 120 м²

Общая площадь 147,36* м² · * размеры приняты, не замерены (реестр — л. 7–9, К-1)

Дизайн-проект интерьера	Стадия	Лист	Листов
	РП	173	175
Спецификация материалов (окончание) М б/м	**Кырлан Александр Сергеевич**		

выпуск 04.11.2026 № 4dfa962484 · стр. 178 из 180

Смета ориентировочная

ПРЕДВАРИТЕЛЬНО · не для производства работ · открыто пунктов: 11 (реестр — л. 7–9)

Работы, материалы, оборудование, услуги и резерв · цены — ориентир по открытым прайсам, не коммерческое предложение

Сводная смета (цены на 21.09.2026, Москва)

№	Наименование работ, материалов, услуг	Ед. изм.	Кол-во	Цена за ед., ₽	Стоимость, ₽			Чей подряд	Срок поставки, дн.	Основание	Источник цены
					план	факт	разница				
Работы — по ведомости объёмов работ											
1	Демонтаж и черновые работы (без 6 поз. по КП)	раздел	1		494 890			бригада, поставщик		ВОР, поз. 1–11; л. 169–171	по ВОР
2	Инженерные системы (без 11 поз. по КП)	раздел	1		230 570			бригада		ВОР, поз. 12–33; л. 169–171	по ВОР
3	Чистовые работы (без 1 поз. по КП)	раздел	1		1 108 128			бригада, поставщик		ВОР, поз. 34–51; л. 169–171	по ВОР
Материалы — по спецификации материалов											
4	Инженерная доска	м²	135,80	4 513	612 865			поставщик		спецификация, поз. 1	Ц7
5	Керамогранит 600×600 мм	м²	14,04	1 800	25 272			поставщик		спецификация, поз. 3	Ц6
6	Керамогранит 600×1200, 1200×600 мм	м²	90,00	3 500	315 000			поставщик		спецификация, поз. 4, 5	Ц6
7	Клей плиточный цементный класса C2 TE S1	меш.	21	1 800	37 800			поставщик		спецификация, поз. 6	Ц7
8	Затирка цементная класса CG2WA	упак.	3	1 000	3 000			поставщик		спецификация, поз. 7	Ц7
9	Краска Tikkurila, банка 2,7 л	банк	36	3 510	126 360			поставщик		спецификация, поз. 23, 24, 26, 30, 32, 33, 34	Ц6
10	Краска Farrow & Ball Modern Emulsion, банка 2,5 л	банк	3	5 800	17 400			поставщик		спецификация, поз. 28, 29	Ц7
11	Плинтус напольный МДФ под покраску	шт	61	368	22 448			поставщик		спецификация, поз. 37, 38	Ц7
12	Прочие материалы с расходом по ТУ (клей для доски, гидроизоляция, демпферная лента, смесь для стяжки, смесь штукатурная гипсовая для машинного и ручного нанесения по маякам, лист гклв 12, профиль стальной оцинкованный 27 × 28 мм: каркас коробов (стойки и направляющие), кабель слаботочки, гофра слаботочки, изделия слаботочки, краска, шпаклёвка, грунтовка, каркас и ГКЛ потолков)	компл	1	по КП				поставщик		спецификация, поз. 2, 8, 9, 10, 11, 12, 13, 14, 15, 16, 17, 18, 19, 20, 21, 22, 25, 27, 31, 35, 36, 39	
Оборудование и мебель — поставка по спецификациям											
13	Кухонный гарнитур по проекту кухни, изготовление и монтаж (4–8 нед.)	компл	1	по КП				поставщик	не задан; ориентир 4–8 нед. от замера	л. 107–110	

Допущения и предложения на листе

Основа листа: взаимное расположение помещений, контур дома 9600 × 8000 и раскладка этажей подобраны проектировщиком под габариты помещений брифа; обмер и проект АР — задание (К-1); высота потолка 2900 мм — по брифу, не замерена; перекрытие 330 мм и отметка 2-го этажа +3,230 приняты; проект КР — задание (К-2); наружные стены 400 мм, перегородки 120 мм приняты (в брифе толщин нет) (К-1); разрешённая мощность 15 кВт принята по типовым ТУ для частного дома (К-4); подрайон климата не задан — принят не северный (жилые от 2,5 м) (К-7).

См. лист открытых вопросов (лист 7, записи К-1, К-2, К-4; лист 8, запись К-7).

Изм.	Кол.уч	Лист	№ док.	Подп.	Дата
Разраб.		Кырлан А.С.			04.11.26
Пров.					
ГИП					
Н. контр.					
Утв.					

ГД-2026-012-АИ

Дом 120 м²

Общая площадь 147,36* м² · * размеры приняты, не замерены (реестр — л. 7–9, К-1)

Дизайн-проект интерьера

Стадия	Лист	Листов
РП	174	175

Смета ориентировочная

М б/м

Кырлан Александр Сергеевич

Смета ориентировочная (окончание)

ПРЕДВАРИТЕЛЬНО · не для производства работ · открыто пунктов: 11 (реестр — л. 7–9)

Работы, материалы, оборудование, услуги и резерв · цены — ориентир по открытым прайсам, не коммерческое предложение

Сводная смета (цены на 21.09.2026, Москва) (продолжение)

№	Наименование работ, материалов, услуг	Ед. изм.	Кол-во	Цена за ед., ₽	Стоимость, ₽			Чей подряд	Срок поставки, дн.	Основание	Источник цены
					план	факт	разница				
14	Двери скрытого монтажа с коробом под покраску, поставка	шт	10	по КП				поставщик	не задан; ориентир ≈ 30 дн.	л. 21–23	
15	Оборудование заказчика слаботочных сетей: точка доступа wi-fi — 2 шт; коммутатор — 1 шт	компл	1	по КП				заказчик		л. 40, 41	
16	Сантехника, светильники, мебель и предметы интерьера	компл	1	по КП				поставщик		л. 63; л. 64, 65; л. 113; л. 29–33	
Прочие работы и услуги											
17	Вынос и вывоз строительного мусора	м³		по факту				бригада		после демонтажа	
18	Подъём материалов на этаж (лифтом или вручную — по договору)	т		по факту				бригада		по массе поставки	
19	Доставка чистовых материалов, 10 % от поставки			10 %	116 015			поставщик		от суммы материалов	
20	Уборка после ремонта	м²	147,36	по факту				бригада		S квартиры	
	Итого работы				**1 833 588**						
	Итого материалы				**1 160 145**						
	Итого прочие услуги				**116 015**						
	Резерв на непредвиденные работы и материалы, 15 %				**466 462**						
	ВСЕГО ориентировочно (без оборудования и позиций по КП)				**3 576 210**						

Примечания

1. Смета ориентировочная, не коммерческое предложение: объёмы — из ведомости объёмов работ и спецификации материалов, цены — нижняя граница открытых прайсов Москвы (цены на 21.09.2026); перед договором цены подтвердить у подрядчика и поставщиков.
2. Источники цен: Ц1 — Домашний мастерок: прайс на отделочные работы, 2026; Ц2 — Домашний мастерок: прайс на плиточные работы, 2026; Ц3 Домашний мастерок: прайс на электромонтажные работы, 2026; Ц4 — Профи ремонтник: штукатурно-малярные работы; Ц5 — Profi.ru: укладка керамогранита на стены, Москва 2026; Ц6 — knowledge/spec-materials.md, разд. 1 и 3: ориентир по сегментам; Ц7 — Розница Москвы, 09.2026: Лемана ПРО, KGSnab, официальный дилер Farrow & Ball.
3. В итог не вошли позиции «по КП» и «по факту»: оборудование и мебель, двери, материалы с расходом по ТУ, вывоз мусора, подъём и уборка.
4. Доставка — 10 % от материалов, резерв — 15 % (частный ремонт 10–20 %) отдельными строками, в количествах не спрятаны. Графы «факт» и «разница» заполняются по актам.

Допущения и предложения на листе

Основа листа: взаимное расположение помещений, контур дома 9600 × 8000 и раскладка этажей подобраны проектировщиком под габариты помещений брифа; обмер и проект АР — задание (К-1); высота потолка 2900 мм — по брифу, не замерена; перекрытие 330 мм и отметка 2-го этажа +3,230 приняты; проект КР — задание (К-2); наружные стены 400 мм, перегородки 120 мм приняты (в брифе толщин нет) (К-1); разрешённая мощность 15 кВт принята по типовым ТУ для частного дома (К-4); подрайон климата не задан — принят не северный (жилые от 2,5 м) (К-7).

См. лист открытых вопросов (лист 7, записи К-1, К-2, К-4; лист 8, запись К-7).

Изм.	Кол.уч	Лист	№ док.	Подп.	Дата
Разраб.		Кырлан А.С.			04.11.26
Пров.					
ГИП					
Н. контр.					
Утв.					

ГД-2026-012-АИ

Дом 120 м²

Общая площадь 147,36* м² · * размеры приняты, не замерены (реестр — л. 7–9, К-1)

Дизайн-проект интерьера	Стадия	Лист	Листов
	РП	175	175

Смета ориентировочная (окончание)

М б/м

Кырлан Александр Сергеевич