
ПРЕДВАРИТЕЛЬНО · не для производства работ · открыто пунктов: 15 (реестр — л. 8–10)

LINEA

ДИЗАЙН-ПРОЕКТ ИНТЕРЬЕРА

Дом 271 м²

Шале

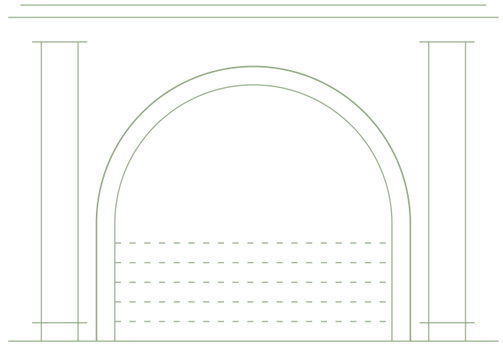

ПАЛИТРА ОТДЕЛКИ

F&B No. 226	Little Greene	NCS S 0804-Y30	NCS S 3040-Y70	F&B No. 93
37 %	30 %	26 %	2 %	1 %

АВТОР ПРОЕКТА

Кырлан Александр Сергеевич

Ноябрь 2026



Квартира сверху · схематичная модель по плану

ОБЩАЯ ПЛОЩАДЬ	ПОМЕЩЕНИЙ	СТАДИЯ	ШИФР	ОСНОВА
270,67 м²	20, из них жилых 6	Рабочий проект · предварительно	ГД-2026-010-АИ	план заказчика, без обмера

Изм.	Кол.уч	Лист	№ док.	Подп.	Дата
Разраб.		Кырлан А.С.			04.11.26
Пров.					
ГИП					
Н. контр.					
Утв.					

ГД-2026-010-АИ

Дом 331 м²

Общая площадь 270,67* м² · * размеры приняты, не замерены (реестр — л. 8–10, К-1)

Дизайн-проект интерьера

Стадия	Лист	Листов
РП	1	216

Титульный лист

М б/м

Кырлан Александр Сергеевич

выпуск 04.11.2026 № 2a77323a49 · стр. 1 из 221

Общие данные

Комплект ГД-2026-010-АИ · Дом 331 м² с мансардой и гаражом

ПРЕДВАРИТЕЛЬНО · не для производства работ · открыто пунктов: 15 (реестр — л. 8–10)

Допущения и предложения на листе. См. лист открытых вопросов (листы 8–10).

Ведомость рабочих чертежей основного комплекта ГД-2026-010-АИ

Лист	Наименование	Примечание
1	Титульный лист	
2	Общие данные	
3	Общие данные	
4	Общие данные	
5	Общие данные	
6	Общие данные	
7	Общие данные	
8	Открытые вопросы, принятые допущения и конфликты. Лист 1 из 3	
9	Открытые вопросы, принятые допущения и конфликты. Лист 2 из 3	
10	Открытые вопросы, принятые допущения и конфликты. Лист 3 из 3	
11	Задание на контрольный обмер и обследование. Лист 1 из 4	
12	Задание на контрольный обмер и обследование. Лист 2 из 4	
13	Задание на контрольный обмер и обследование. Лист 3 из 4	
14	Задание на контрольный обмер и обследование. Лист 4 из 4	
15	График закупок и работ. Лист 1 из 4	
16	График закупок и работ. Лист 2 из 4	
17	График закупок и работ. Лист 3 из 4	
18	График закупок и работ. Лист 4 из 4	
19	Обмерный план · 1-й этаж	
20	Обмерный план · Мансарда	
21	План демонтажа и монтажа перегородок · 1-й этаж	
22	План демонтажа и монтажа перегородок · Мансарда	
23	План дверей · 1-й этаж	
24	План дверей · Мансарда	
25	Ведомость заполнения проёмов	
26	Схемы дверных блоков	
27	Лестница Л-1	
28	Концепция интерьера · 1-й этаж	
29	Концепция интерьера · Мансарда	
30	План расстановки мебели · 1-й этаж	

Ведомость рабочих чертежей основного комплекта ГД-2026-010-АИ (продолжение)

Лист	Наименование	Примечание
31	План расстановки мебели · Мансарда	
32	Спецификация мебели и оборудования	
33	Спецификация мебели и оборудования (продолжение)	
34	Спецификация мебели и оборудования (продолжение)	
35	Спецификация мебели и оборудования (продолжение)	
36	Спецификация мебели и оборудования (продолжение)	
37	План розеток и электровыводов · 1-й этаж	
38	План розеток и электровыводов · Мансарда	
39	План освещения · 1-й этаж	
40	План освещения · Мансарда	
41	План выключателей и схема включения · 1-й этаж	
42	План выключателей и схема включения · Мансарда	
43	Ведомость электроточек и изделий	
44	Ведомость электроточек и изделий (продолжение)	
45	Ведомость электроточек и изделий (продолжение)	
46	Однолинейная схема щита	
47	Однолинейная схема щита (продолжение)	
48	План принципиальных трасс · 1-й этаж	
49	План принципиальных трасс · Мансарда	
50	План слаботочных сетей · 1-й этаж	
51	План слаботочных сетей · Мансарда	
52	План вентиляции · 1-й этаж	
53	План вентиляции · Мансарда	

Общие указания — лист 7: ±0,000 — чистый пол 1-го этажа; несущие конструкции и сети — по отдельному проекту; скрытые работы — по актам. Вопросы и допущения — листы 8–10.

Изм.	Кол.уч	Лист	№ док.	Подп.	Дата
Разраб.		Кырлан А.С.			04.11.26
Пров.					
ГИП					
Н. контр.					
Утв.					

ГД-2026-010-АИ

Дом 331 м²

Общая площадь 270,67* м² · * размеры приняты, не замерены (реестр — л. 8–10, К-1)

Дизайн-проект интерьера

Стадия	Лист	Листов
РП	2	216

Общие данные

М б/м

Кырлан Александр Сергеевич

выпуск 04.11.2026 № 2a77323a49 · стр. 2 из 221

Общие данные

Комплект ГД-2026-010-АИ · лист 2 общих данных (продолжение)

Допущения и предложения на листе. См. лист открытых вопросов (листы 8–10).

Ведомость рабочих чертежей основного комплекта ГД-2026-010-АИ (продолжение)

Лист	Наименование	Примечание
54	План отопления · 1-й этаж	
55	План отопления · Мансарда	
56	План выводов сантехники · 1-й этаж	
57	План выводов сантехники · Мансарда	
58	Схема разводки водопровода и канализации · 1-й этаж	
59	Схема разводки водопровода и канализации · Мансарда	
60	Аксонометрическая схема В1 (холодное водоснабжение)	
61	Аксонометрическая схема Т3 (горячее водоснабжение)	
62	Аксонометрическая схема К1 (канализация)	
63	Развёртки мокрых зон: выводы ВК. Кухня-столовая	
64	Развёртки мокрых зон: выводы ВК. Санузел 1 этажа (лист 1 из 2)	
65	Развёртки мокрых зон: выводы ВК. Санузел 1 этажа (лист 2 из 2)	
66	Развёртки мокрых зон: выводы ВК. Санузел мастер (лист 1 из 2)	
67	Развёртки мокрых зон: выводы ВК. Санузел мастер (лист 2 из 2)	
68	Развёртки мокрых зон: выводы ВК. Санузел 2 (лист 1 из 2)	
69	Развёртки мокрых зон: выводы ВК. Санузел 2 (лист 2 из 2)	
70	Спецификация сантехнического оборудования	
71	Техническое задание на подбор светильников	
72	Техническое задание на подбор светильников (продолжение)	
73	План потолков · 1-й этаж	
74	План потолков · Мансарда	
75	Разрезы и узлы потолков	
76	Разрезы и узлы потолков (продолжение)	
77	Разрезы и узлы потолков (продолжение)	
78	Разрезы и узлы потолков (продолжение)	
79	Сечения потолков М 1:10	
80	Сечения потолков М 1:10	
81	Сечения потолков М 1:10	
82	Раскладка плитки. Планы полов	
83	Раскладка плитки. Котельная. Прихожая. Тамбур	

Ведомость рабочих чертежей основного комплекта ГД-2026-010-АИ (продолжение)

Лист	Наименование	Примечание
84	Раскладка плитки. Веранда. Крыльцо	
85	Раскладка плитки. Санузел 1 этажа. Развёртки стен	
86	Раскладка плитки. Санузел мастер. Развёртки стен	
87	Раскладка плитки. Санузел 2. Развёртки стен	
88	План полов · 1-й этаж	
89	План полов · Мансарда	
90	Конструкции полов и стыки покрытий	
91	Ведомость отделки помещений. Лист 1 из 4	
92	Ведомость отделки помещений. Лист 2 из 4	
93	Ведомость отделки помещений. Лист 3 из 4	
94	Ведомость отделки помещений. Лист 4 из 4	
95	Колерная карта	
96	Колерная карта	
97	Спецификация отделочных материалов	
98	Спецификация отделочных материалов	
99	Концепция декора и визуализации	
100	План текстиля и декора · 1-й этаж	
101	План текстиля и декора · Мансарда	
102	Шторы и карнизы	
103	Ведомость текстиля	
104	Ведомость текстиля (продолжение)	
105	Ведомость декора	
106	Схемы развески	

Общие указания — лист 7: ±0,000 — чистый пол 1-го этажа; несущие конструкции и сети — по отдельному проекту; скрытые работы — по актам. Вопросы и допущения — листы 8–10.

Изм.	Кол.уч	Лист	№ док.	Подп.	Дата
Разраб.		Кырлан А.С.			04.11.26
Пров.					
ГИП					
Н. контр.					
Утв.					

ГД-2026-010-АИ

Дом 331 м²

Общая площадь 270,67* м² · * размеры приняты, не замерены (реестр — л. 8–10, К-1)

Дизайн-проект интерьера

Стадия	Лист	Листов
РП	3	216

Общие данные

М б/м

Кырлан Александр Сергеевич

выпуск 04.11.2026 № 2a77323a49 · стр. 3 из 221

Общие данные

Комплект ГД-2026-010-АИ · лист 3 общих данных (продолжение)

Допущения и предложения на листе. См. лист открытых вопросов (листы 8–10).

Ведомость рабочих чертежей основного комплекта ГД-2026-010-АИ (продолжение)

Лист	Наименование	Примечание
107	Схемы развески (продолжение)	
108	Встроенная мебель. Схема расположения · 1-й этаж	
109	Встроенная мебель. Схема расположения · Мансарда	
110	Система хранения Кт1	
111	Система хранения Кл1	
112	Шкаф-купе Пх1	
113	Система хранения Гр1	
114	Система хранения Гм2	
115	Шкаф распашной С3	
116	Система хранения Сп3	
117	Шкаф распашной Дт3	
118	Шкаф распашной Дт6	
119	Кухня (пом. 1). Развёртка гарнитура	
120	Кухня (пом. 1). Монтажная схема	
121	Остров Кх7 (пом. 1). Чертёж изделия	
122	Шкафы. Монтажная схема. Лист 1 из 2	
123	Шкафы. Монтажная схема. Лист 2 из 2	
124	Ведомости изделий, техники и фурнитуры	
125	Реестр марок отделки и позиций альбома	
126	Реестр марок отделки и позиций альбома (продолжение)	
127	Схема расположения развёрток и узлов · 1-й этаж	
128	Схема расположения развёрток и узлов · Мансарда	
129	Развёртка стены А. Кухня-столовая (пом. 1), кухонный фронт	
130	Привязки электроточек и выводов ВК, стена А. Кухня-столовая (пом. 1)	
131	Развёртка стены Б. Кухня-столовая (пом. 1)	
132	Развёртка стены В. Кухня-столовая (пом. 1)	
133	Развёртка стены Г. Кухня-столовая (пом. 1)	
134	Развёртка стены А. Кабинет-гостевая (пом. 2)	
135	Привязки электроточек, стена А. Кабинет-гостевая (пом. 2)	
136	Развёртка стены Б. Кабинет-гостевая (пом. 2)	

Ведомость рабочих чертежей основного комплекта ГД-2026-010-АИ (продолжение)

Лист	Наименование	Примечание
137	Развёртка стены В. Кабинет-гостевая (пом. 2)	
138	Привязки электроточек, стена В. Кабинет-гостевая (пом. 2)	
139	Развёртка стены Г. Кабинет-гостевая (пом. 2)	
140	Развёртки стен А, Б. Санузел 1 этажа (пом. 3)	
141	Привязки выводов ВК, стена А. Санузел 1 этажа (пом. 3)	
142	Развёртки стен В, Г. Санузел 1 этажа (пом. 3)	
143	Развёртки стен А, Б. Котельная (пом. 4)	
144	Развёртка стены Г. Котельная (пом. 4)	
145	Развёртка стены А. Гостиная (пом. 5)	
146	Привязки электроточек, стена А. Гостиная (пом. 5)	
147	Развёртка стены Б. Гостиная (пом. 5)	
148	Развёртка стены В. Гостиная (пом. 5)	
149	Развёртка стены Г. Гостиная (пом. 5)	
150	Развёртка стены А. Холл с лестницей (пом. 6)	
151	Развёртка стены В. Холл с лестницей (пом. 6)	
152	Развёртки стен. Кладовая (пом. 7)	
153	Развёртка стены А. Прихожая (пом. 8)	
154	Развёртка стены Б. Прихожая (пом. 8)	
155	Развёртки стен В, Г. Прихожая (пом. 8)	
156	Привязки электроточек, стена Г. Прихожая (пом. 8)	
157	Развёртки стен. Тамбур (пом. 9)	
158	Развёртка стены А. Гараж (пом. 10)	
159	Развёртка стены Б. Гараж (пом. 10)	

Общие указания — лист 7: ±0,000 — чистый пол 1-го этажа; несущие конструкции и сети — по отдельному проекту; скрытые работы — по актам. Вопросы и допущения — листы 8–10.

Изм.	Кол.уч	Лист	№ док.	Подп.	Дата
Разраб.		Кырлан А.С.			04.11.26
Пров.					
ГИП					
Н. контр.					
Утв.					

ГД-2026-010-АИ

Дом 331 м²

Общая площадь 270,67* м² · * размеры приняты, не замерены (реестр — л. 8–10, К-1)

Дизайн-проект интерьера

Стадия	Лист	Листов
РП	4	216

Общие данные

М б/м

Кырлан Александр Сергеевич

выпуск 04.11.2026 № 2a77323a49 · стр. 4 из 221

Общие данные

Комплект ГД-2026-010-АИ · лист 4 общих данных (продолжение)

Допущения и предложения на листе. См. лист открытых вопросов (листы 8–10).

Ведомость рабочих чертежей основного комплекта ГД-2026-010-АИ (продолжение)

Лист	Наименование	Примечание
160	Развёртка стены Б: схема и ведомость отделки. Гараж (пом. 10)	
161	Развёртка стены В. Гараж (пом. 10)	
162	Развёртка стены Г. Гараж (пом. 10)	
163	Развёртка стены Г: схема и ведомость отделки. Гараж (пом. 10)	
164	Развёртка стены А. Веранда (пом. 11)	
165	Развёртка стены В. Веранда (пом. 11)	
166	Развёртка стены Г. Веранда (пом. 11)	
167	Развёртки стен. Крыльцо (пом. 12)	
168	Развёртка стены А. Спальня мастер (пом. 13)	
169	Привязки электроточек, стена А. Спальня мастер (пом. 13)	
170	Развёртка стены Б. Спальня мастер (пом. 13)	
171	Развёртка стены В. Спальня мастер (пом. 13)	
172	Развёртка стены Г. Спальня мастер (пом. 13)	
173	Развёртки стен А, Б. Гардеробная мастер (пом. 14)	
174	Развёртки стен В, Г. Гардеробная мастер (пом. 14)	
175	Развёртки стен А, Б. Санузел мастер (пом. 15)	
176	Развёртки стен В, Г. Санузел мастер (пом. 15)	
177	Привязки электроточек и выводов ВК, стены А, В. Санузел мастер (пом. 15)	
178	Развёртка стены А. Спальня 2 (пом. 16)	
179	Привязки электроточек, стена А. Спальня 2 (пом. 16)	
180	Развёртка стены Б. Спальня 2 (пом. 16)	
181	Развёртка стены В. Спальня 2 (пом. 16)	
182	Привязки электроточек, стена В. Спальня 2 (пом. 16)	
183	Развёртка стены Г. Спальня 2 (пом. 16)	
184	Развёртка стены А. Холл мансарды (пом. 17)	
185	Развёртка стены Б. Холл мансарды (пом. 17)	
186	Развёртка стены Б: схема и ведомость отделки. Холл мансарды (пом. 17)	
187	Развёртка стены В. Холл мансарды (пом. 17)	
188	Развёртка стены Г. Холл мансарды (пом. 17)	

Ведомость рабочих чертежей основного комплекта ГД-2026-010-АИ (продолжение)

Лист	Наименование	Примечание
189	Развёртка стены Г: схема и ведомость отделки. Холл мансарды (пом. 17)	
190	Развёртка стены А. Спальня 3 (пом. 18)	
191	Развёртка стены Б. Спальня 3 (пом. 18)	
192	Развёртка стены В. Спальня 3 (пом. 18)	
193	Привязки электроточек, стена В. Спальня 3 (пом. 18)	
194	Развёртка стены Г. Спальня 3 (пом. 18)	
195	Развёртка стены А. Спальня 4 (пом. 19)	
196	Развёртка стены Б. Спальня 4 (пом. 19)	
197	Развёртка стены В. Спальня 4 (пом. 19)	
198	Привязки электроточек, стена В. Спальня 4 (пом. 19)	
199	Развёртка стены Г. Спальня 4 (пом. 19)	
200	Развёртки стен А, Б. Санузел 2 (пом. 20)	
201	Привязки электроточек и выводов ВК, стена А. Санузел 2 (пом. 20)	
202	Привязки электроточек и выводов ВК, стена Б. Санузел 2 (пом. 20)	
203	Развёртки стен В, Г. Санузел 2 (пом. 20)	
204	Привязки электроточек и выводов ВК, стена В. Санузел 2 (пом. 20)	
205	Узлы. Лист 1 из 2	
206	Узлы. Лист 2 из 2	
207	Ведомость объёмов работ	
208	Ведомость объёмов работ (продолжение)	
209	Ведомость объёмов работ (продолжение)	
210	Ведомость объёмов работ (продолжение)	
211	Ведомость объёмов работ (окончание)	

Общие указания — лист 7: ±0,000 — чистый пол 1-го этажа; несущие конструкции и сети — по отдельному проекту; скрытые работы — по актам. Вопросы и допущения — листы 8–10.

Изм.	Кол.уч	Лист	№ док.	Подп.	Дата
Разраб.		Кырлан А.С.			04.11.26
Пров.					
ГИП					
Н. контр.					
Утв.					

ГД-2026-010-АИ

Дом 331 м²

Общая площадь 270,67* м² · * размеры приняты, не замерены (реестр — л. 8–10, К-1)

Дизайн-проект интерьера

Стадия	Лист	Листов
РП	5	216

Общие данные

М б/м

Кырлан Александр Сергеевич

выпуск 04.11.2026 № 2a77323a49 · стр. 5 из 221

Общие данные

Комплект ГД-2026-010-АИ · лист 5 общих данных (продолжение)

Ведомость рабочих чертежей основного комплекта ГД-2026-010-АИ (продолжение)

Лист	Наименование	Примечание
212	Спецификация материалов	
213	Спецификация материалов (продолжение)	
214	Спецификация материалов (окончание)	
215	Смета ориентировочная	
216	Смета ориентировочная (окончание)	

Ведомость ссылочных и прилагаемых документов

Обозначение	Наименование	Примечание
	Ссылочные документы	
ГОСТ 21.201-2011	СПДС. Условные графические изображения элементов зданий, сооружений и конструкций	
ГОСТ 21.205-2016	СПДС. Условные обозначения элементов санитарно-технических систем	
ГОСТ 21.210-2014	СПДС. Изображения условные графические электрооборудования и проводок на планах	
ГОСТ 2.306-68	ЕСКД. Обозначения графические материалов и правила их нанесения на чертежах	
	Прилагаемые документы	
ГД-2026-010-АИ.В1	Визуализация. Вид сверху (3D): планировка с мебелью, текстилем и декором	альбом визуализаций
ГД-2026-010-АИ.В2	Визуализация. Вид сверху (3D): планировка с мебелью, текстилем и декором	
ГД-2026-010-АИ.В3	Визуализация. Интерьер: Веранда (пом. 11), стена В	
ГД-2026-010-АИ.В4	Визуализация. Интерьер: Санузел 1 этажа (пом. 3), общий вид	
ГД-2026-010-АИ.В5	Визуализация. Интерьер: Санузел мастер (пом. 15), общий вид	
ГД-2026-010-АИ.В6	Визуализация. Интерьер: Санузел 2 (пом. 20), общий вид	
ГД-2026-010-АИ.В7	Визуализация. Интерьер: Спальня мастер (пом. 13), стена А	
ГД-2026-010-АИ.В8	Визуализация. Интерьер: Спальня мастер (пом. 13), стена В	
ГД-2026-010-АИ.В9	Визуализация. Интерьер: Спальня 2 (пом. 16), стена А	
ГД-2026-010-АИ.В10	Визуализация. Интерьер: Спальня 2 (пом. 16), стена Б	
ГД-2026-010-АИ.В11	Визуализация. Интерьер: Холл с лестницей (пом. 6), общий вид	
ГД-2026-010-АИ.В12	Визуализация. Интерьер: Холл мансарды (пом. 17), общий вид	
ГД-2026-010-АИ.В13	Визуализация. Интерьер: Прихожая (пом. 8), стена А	
ГД-2026-010-АИ.В14	Визуализация. Интерьер: Прихожая (пом. 8), стена Б	

Общие указания — лист 7: ±0,000 — чистый пол 1-го этажа; несущие конструкции и сети — по отдельному проекту; скрытые работы — по актам. Вопросы и допущения — листы 8–10.

Ведомость ссылочных и прилагаемых документов (продолжение)

Обозначение	Наименование	Примечание
ГД-2026-010-АИ.В15	Визуализация. Интерьер: Спальня 3 (пом. 18), стена А	
ГД-2026-010-АИ.В16	Визуализация. Интерьер: Спальня 3 (пом. 18), стена В	
ГД-2026-010-АИ.В17	Визуализация. Интерьер: Спальня 4 (пом. 19), стена А	
ГД-2026-010-АИ.В18	Визуализация. Интерьер: Спальня 4 (пом. 19), стена В	
ГД-2026-010-АИ.В19	Визуализация. Интерьер: Кухня-столовая (пом. 1), стена А	
ГД-2026-010-АИ.В20	Визуализация. Интерьер: Кухня-столовая (пом. 1), стена Г	
ГД-2026-010-АИ.В21	Визуализация. Интерьер: Гостиная (пом. 5), стена А	
ГД-2026-010-АИ.В22	Визуализация. Интерьер: Гостиная (пом. 5), стена В	
ГД-2026-010-АИ.В23	Визуализация. Интерьер: Гостиная (пом. 5), стена Г	
ГД-2026-010-АИ.В24	Визуализация. Интерьер: Кабинет-гостевая (пом. 2), стена А	
ГД-2026-010-АИ.В25	Визуализация. Интерьер: Кабинет-гостевая (пом. 2), стена Г	
ГД-2026-010-АИ.В26	Визуализация. Интерьер: Гардеробная мастер (пом. 14), общий вид	

Допущения и предложения на листе

Основа листа: размеры и контуры этажей подобраны проектировщиком по составу помещений и площадям этажей с картинки 470 px (размеры на ней не читаются); обмер и исходный проект — задание (К-1); высоты: 1-й этаж 2800 мм, мансарда 2700 мм (горизонтальная часть) приняты; скаты кровли мансарды приняты по картинке: колено 1200 мм, уклон 45°, конёк вдоль длинной стороны; проект КР — задание (К-2); наружные стены 400 мм, перегородки 120 мм приняты (К-1); разрешённая мощность 15 кВт принята по типовым ТУ для частного дома (К-4); подрайон климата не задан — принят не северный (жилые от 2,5 м) (К-7).

См. лист открытых вопросов (лист 8, записи К-1, К-2, К-4, К-7).

Изм.	Кол.уч	Лист	№ док.	Подп.	Дата
Разраб.		Кырлан А.С.			04.11.26
Пров.					
ГИП					
Н. контр.					
Утв.					

ГД-2026-010-АИ

Дом 331 м²

Общая площадь 270,67* м² · * размеры приняты, не замерены (реестр — л. 8–10, К-1)

Дизайн-проект интерьера

Стадия	Лист	Листов
РП	6	216

Общие данные

М б/м

Кырлан Александр Сергеевич

выпуск 04.11.2026 № 2a77323a49 · стр. 6 из 221

Общие данные

Комплект ГД-2026-010-АИ · лист 6 общих данных (продолжение)

Состав дизайн-проекта

Раздел	Состав	Листы
Обложка	Дизайн-проект интерьера; Дом 331 м²; автор проекта — Кырлан Александр Сергеевич	1 с.
Концепция	Стиль Шале 60 % + Эко и органический модерн 40 %: концепция интерьера, палитра и материалы (колерная карта — лист 95)	л. 28
Визуализации	26 изобр.: Вид сверху (3D): планировка с мебелью, текстилем и декором; Вид сверху (3D): планировка с мебелью, текстилем и декором; Веранда, стена В; Санузел 1 этажа, общий вид; Санузел мастер, общий вид; Санузел 2, общий вид; Спальня мастер, стена А; Спальня мастер, стена В; Спальня 2, стена А; Спальня 2, стена Б; Холл с лестницей, общий вид; Холл мансарды, общий вид; Прихожая, стена А; Прихожая, стена Б; Спальня 3, стена А; Спальня 3, стена В; Спальня 4, стена А; Спальня 4, стена В; Кухня-столовая, стена А; Кухня-столовая, стена Г; Гостиная, стена А; Гостиная, стена В; Гостиная, стена Г; Кабинет-гостевая, стена А; Кабинет-гостевая, стена Г; Гардеробная мастер, общий вид	В1–В26
Рабочие чертежи	планы, развёртки, узлы (развёртки и узлы — листы 63–69, 127, 128, 140, 142, 143, 152, 155, 157, 167, 173–176, 200, 203, 205, 206)	л. 1–216
Спецификации и ведомости	оборудование, изделия, отделка, электроточки	л. 25, 32–36, 43–45, 70, 91–98, 103–105, 160, 163, 186, 189, 207–214

Условные обозначения

- контрольный отрезок 1000 мм натуры: по нему проверяют печать 1:1
- отметка уровня, м: ±0,000 — чистый пол 1-го этажа
- А — марка развёртки: буква стены, стрелка — взгляд
- О1 — марка отделки по реестру отделки альбома
- выноска узла: над полкой — узел, под полкой — лист

Общие указания

1. Рабочие чертежи интерьера разработаны на основании задания на проектирование и обмерного плана (лист 19). Объект: Дом 331 м²; автор проекта — Кырлан Александр Сергеевич; общая площадь 270,67 м², жилая 119,16 м², помещений 18.
2. Рабочие чертежи выполнены в соответствии с заданием на проектирование и нормативными документами, перечисленными в п. 4.
3. Открытые вопросы, принятые допущения и конфликты между разделами, не снятые к выпуску комплекта, сведены в таблицы на листах 8–10. До ответа по пункту таблицы показанное на указанном там листе — допущение, а не утверждённое решение: комплект по этим листам предварительный.
4. Нормативные документы, на которые есть ссылки в листах комплекта: ГОСТ Р 21.101-2026; ГОСТ 21.501-2018; ГОСТ 2.302-68; ГОСТ 2.303-68; ГОСТ 2.304-81; ГОСТ 2.307-2011; СП 54.13330.2022; СП 71.13330.2017; СП 73.13330.2016; ПУЭ (7-е изд.), гл. 1.8, 7.1; ГОСТ Р 50571.7.701-2024; СанПиН 1.2.3685-21; ГОСТ 2.702; ГОСТ 2.755; ГОСТ 21.110-2013; ГОСТ 21.601; ГОСТ 475-2016; ГОСТ 13996-2019; ГОСТ 23166-2021; ГОСТ 25772-2025; ГОСТ 31173-2016; ГОСТ 31565-2012; ГОСТ 32414-2013; ГОСТ 32415-2013; ГОСТ Р 56387-2018; СП 20.13330.2016; СП 29.13330.2011; СП 30.13330.2020; СП 51.13330.2011; СП 55.13330.2016; СП 59.13330.2020; СП 62.13330; СП 131.13330. Документы из ведомости ссылочных документов здесь не повторяются.
5. За отметку ±0,000 принят уровень чистого пола 1-го этажа дома (условная нулевая отметка; абсолютная — по проекту дома); отметки чистого пола этажей: мансарда +3,150 — отметки уровней этажа на листах даны от ±0,000 здания. Отметка чистого пола мокрых помещений — −0,015, +3,135. Размеры — в миллиметрах, отметки — в метрах, площади — в м²; высоты установки Н — от чистого пола своего помещения до оси изделия.
6. Несущие конструкции, общедомовые стояки, вентиляционные каналы и инженерные сети дома настоящим комплектом не изменяются. Работы, затрагивающие их (проём или штраба в несущей стене, перенос стояка, врезка в вентканал, расширение мокрой зоны), выполняются только по отдельному проекту, к которому прилагается техническое заключение о допустимости и безопасности работ, выданное автором проекта дома или организацией с допуском на обследование, и который согласован в установленном порядке (Жилищный кодекс РФ, ст. 25–29).
7. Трассы инженерных сетей на листах — принципиальные. Расчёты электрических нагрузок и токов КЗ, гидравлики, воздухообмена, освещённости и нагрузок на перекрытие выполняются в проектах ЭОМ, ВК, ОВ и КР организацией с допуском СРО; фактические трассы до закрытия отделкой фиксируются исполнительными схемами.
8. Стиль интерьера — Шале 60 % + Эко и органический модерн 40 %. Палитра проекта: основной 60 % — Farrow & Ball No. 226 «Joa's White», NCS S 0804-Y30R «S 0804-Y30R», Little Greene No. 105 «Slaked Lime»; дополнительный 30 % — Tikkurila V451 «Olive grove V451», NCS S 3020-G30Y «S 3020-G30Y», Tikkurila X463 «Sandstone X463», Farrow & Ball No. 229 «Elephant's Breath — тёплый средне-серый с лиловым подтоном», Farrow & Ball No. 40 «Mouse's Back — тёплый коричнево-серый», Farrow & Ball No. 243 «Charleston Gray — серо-коричневый «камень»», NCS S 2005-Y20R «Светлый песочно-серый», NCS S 3010-Y30R «S 3010-Y30R»; акцент 10 % — NCS S 7020-G10Y «Хвойный тёмно-зелёный», Farrow & Ball No. 64 «Red Earth», Farrow & Ball No. 43 «Eating Room Red — брусничный красный». Коды цвета — по веерам производителей; цвет утверждается по выкрасу на объекте при освещении проекта.
9. Площади поверхностей — по чистым граням стен до отделки: стены = периметр × высоту от чистого пола помещения до низа потолка минус проёмы (облицовка плиткой — до верха облицовки); плинтус = периметр минус дверные проёмы; пол и потолок — по площади помещения. Количество плиток — по раскладке. Способ один для всех листов комплекта (ведомость отделки, колерная карта, раскладка плитки, развёртки).
10. Марки: стены помещения на всех листах — А (верхняя по плану), Б (правая), В (нижняя), Г (левая); марка отделки О — одна на весь альбом; реестр марок отделки (с позициями колерной карты той же отделки) и марки позиций по видам — на листе 125.
11. Развёртки стен выполнены по всем помещениям для стен с электроточками, мебелью, декором и отделкой: санузлы и кухонный фронт — в М 1:25, остальные стены — в М 1:50; расположение развёрток и узлов — на листе 127, узлы — на листе 205.
12. Перечень скрытых работ, на которые составляются акты освидетельствования (форма по приказу Минстроя России № 344/пр): гидроизоляция пола и стен мокрых помещений (с тестом проливом); стяжка пола (толщина, прочность, влажность основания); звукоизоляционные слои и демпферная лента; скрытая электропроводка (за потолком и в штробах стен; условия штробления — в следующем пункте); трубопроводы водоснабжения и канализации до закрытия (опрессовка, уклоны); закладные и усиления под подвесные приборы, мебель и тяжёлый декор, рамы инсталляций; короба дверей скрытого монтажа до штукатурки; каркасы ГКЛ потолков, коробов и перегородок до обшивки.
13. Скрытая электропроводка: за потолком и в штробах стен. Штробы в стенах выполняются только после технического заключения о несущих конструкциях; до заключения несущие стены не определены, и все стены считаются несущими; объём штроб — в ведомости объёмов работ, строка «Штробы в стенах» (вертикальные спуски; объём не меньше фактического, горизонтальные трассы — по исполнительной схеме).
14. Критерии приёмки: допуски отделочных покрытий — по СП 71.13330.2017; испытания систем водоснабжения и канализации — по СП 73.13330.2016 до закрытия трасс; приёмо-сдаточные испытания электроустановки — по ПУЭ, гл. 1.8, с протоколом электролаборатории.
15. Осознанные отступления от ГОСТ Р 21.101-2026, принятые в комплекте: номер листа и число листов («Листов») указаны на каждом листе; на масштабных листах в основной надписи указан фактический масштаб и дан контрольный отрезок 1000 мм; развёртки стен выполнены в М 1:25 (ГОСТ 21.507-81 — 1:50…1:500) ради читаемости привязок; размерные числа и марки элементов (Д-1, ОК-1, О6) кеглем 2,5 мм, номера помещений — в кружке Ø 8 мм (канон — 3,5 мм и Ø 12 мм): так насыщенные листы А3 читаются без наложений надписей.
16. Графы «Пров.», «Н. контр.», «Утв.» основной надписи заполняются при согласовании комплекта с заказчиком; до согласования комплект подписывает автор проекта (графа «Разраб.»).

Допущения и предложения на листе

Основа листа: размеры и контуры этажей подобраны проектировщиком по составу помещений и площадям этажей с картинки 470 px (размеры на ней не читаются); обмер и исходный проект — задание (К-1); высоты: 1-й этаж 2800 мм, мансарда 2700 мм (горизонтальная часть) приняты; скаты кровли мансарды приняты по картинке: колено 1200 мм, уклон 45°, конёк вдоль длинной стороны; проект КР — задание (К-2); наружные стены 400 мм, перегородки 120 мм приняты (К-1); разрешённая мощность 15 кВт принята по типовым ТУ для частного дома (К-4); подрайон климата не задан — принят не северный (жилые от 2,5 м) (К-7).
См. лист открытых вопросов (лист 8, записи К-1, К-2, К-4, К-7).

Изм.	Кол.уч	Лист	№ док.	Подп.	Дата	ГД-2026-010-АИ			
						Дом 331 м²			
						Общая площадь 270,67* м² · * размеры приняты, не замерены (реестр — л. 8–10, К-1)			
Разраб.		Кырлан А.С.			04.11.26	Дизайн-проект интерьера	Стадия	Лист	Листов
Пров.							РП	7	216
ГИП									
						Общие данные	Кырлан Александр Сергеевич		
Н. контр.						М б/м			
Утв.									

выпуск 04.11.2026 № 2a77323a49 · стр. 7 из 221

Открытые вопросы, принятые допущения и конфликты. Лист 1 из 3

Сводка по реестрам координации (стартовое совещание 18.10.2026)

Комплект предварительный по пунктам этих таблиц. Пока по пункту нет ответа или решения, показанное на указанном листе — допущение проектировщика, а не утверждённое решение.
Сводка: открытых вопросов — 12 (из них ждут факта объекта — 7: контрольного обмера, обследования или документа); конфликтов между разделами — 1; изменений в реестре — 2, из них без подписи — 2.
Пункты, ответ на которые лежит на объекте, а не за столом проектировщика (графа «Вид», строка «Ждёт»), собраны на листе «Задание на контрольный обмер и обследование» (листы 11–14): что и где замерить, с какой точностью и чем подтвердить. Пункты, ждущие решения человека, на объекте не закрываются.

Открытые вопросы и принятые допущения

№	Формулировка	Вид	Кто решает	Если решения нет	Лист, где это проявляется
К-1	Размеры дома на картинке заказчика (470 px) не читаются: состав помещений и форма сняты с картинки, размеры подобраны проектировщиком под площади этажей 185,80 и 145,73 м². Нужен исходный проект дома (АР) или обмер.	Отсутствует Ждёт: обмера	Архитектор-планировщик	размеры на листах — предложение проектировщика; мебель на заказ и материалы по ним не заказывать	л. 19, 20 — Обмерный план л. 19, 21, 23, 28, 30, 37, 39, 41, 48, 50, 52, 54, 56, 58, 64, 65, 73, 85, 88, 100, 108, 127, 140–142 1-й этаж л. 30, 31 — План расстановки мебели л. 19, 21, 23, 28, 30, 37, 39, 41, 48, 50, 52, 54, 56, 58, 64, 65, 73, 85, 88, 100, 108, 127, 140–142 1-й этаж
К-2	Высоты этажей и кровля не известны: приняты 2800 мм (1-й этаж) и 2700 мм (горизонтальная часть потолка мансарды); скаты двускатная кровля, конёк вдоль длинной стороны, колено 1200 мм, уклон 45° (по перспективе и фасаду с картинки).	Отсутствует	Архитектор-планировщик	высоты — принятые, уточнить по проекту АР	л. 19, 20 — Обмерный план л. 19, 21, 23, 28, 30, 37, 39, 41, 48, 50, 52, 54, 56, 58, 64, 65, 73, 85, 88, 100, 108, 127, 140–142 1-й этаж л. 73, 74 — План потолков л. 19, 21, 23, 28, 30, 37, 39, 41, 48, 50, 52, 54, 56, 58, 64, 65, 73, 85, 88, 100, 108, 127, 140–142 1-й этаж
К-4	Разрешённая мощность дома по ТУ неизвестна, принята 15 кВт.	Отсутствует	Инженер-электрик	щит и группы рассчитаны на 15 кВт; при меньших ТУ пересчёт	л. 46 — Однолинейная схема щита л. 37, 38 — План розеток и электровыводов л. 19, 21, 23, 28, 30, 37, 39, 41, 48, 50, 52, 54, 56, 58, 64, 65, 73, 85, 88, 100, 108, 127, 140–142 1-й этаж
К-5	Планировка этажей — предложение проектировщика по составу помещений с картинки (несущие стены, лестница, перекрытие не известны): нужен проект АР/КР дома.	Отсутствует Ждёт: документа	Архитектор-планировщик	перегородки и проёмы — предложение, к строительству не выдаются	л. 19, 20 — Обмерный план л. 19, 21, 23, 28, 30, 37, 39, 41, 48, 50, 52, 54, 56, 58, 64, 65, 73, 85, 88, 100, 108, 127, 140–142 1-й этаж
К-6	Лестница Л-1 на картинке заказчика — одномаршевая в холле 1-го этажа (3,0×3,6 м), видно 11 проступей. До пола мансарды +3,150 нужно 18 подъёмов по 175 мм (равные ступени — СП 55.13330.2016 п. 8.2), то есть 17 проступей по 280 мм = 4,76 м длины марша; в холл 3,48 м в свету одномаршевая не встаёт (не хватает 1,66 м). Варианты: Г-образная с 3 забежными ступенями (8 + 3 + 6 подъёмов по 175 — встаёт в холл 3,24×2,68 м; при детях забежные — компромисс), Г-образная с площадкой (9 + 7 подъёмов по 197 мм — круче практики 150–180, для дома допустимо: уклон не нормируется, СП 55 п. 7.5), перенос лестницы или иная высота этажа по проекту АР/КР. Нужны: решение по типу марша и проект АР/КР (высота этажа, перекрытие, проём). На плане 1-го этажа марш по картинке стоит вдоль стены холла с проёмом Пр-2 из гостиной и перекрывает его: в любом варианте Пр-2 освободить (сдвинуть проём или марш); на монтажных планах обоих этажей марш и проём перекрытия показаны по принятому габариту до решения.	Отсутствует Ждёт: обмера, затем решения	Архитектор-планировщик	марш на планах и лист «Лестница Л-1» — по картинке (11 проступей, до отм. +2,100), ограждение и проём считаются по этому габариту; изделие не заказывать, проём в перекрытии не резать	architect/stairs-л-1 (лист по названию не найден)
К-7	Климатический подрайон (СП 131.13330) не задан: принят не северный — жилые комнаты и кухня под потолком от 2,5 м (СП 54, п. 5.12); в IA, IБ, IГ, IД, IVA — от 2,7 м.	Отсутствует Ждёт: документа	Архитектор-планировщик	отметки потолков жилых — по 2,5 м; при северном подрайоне уровни ниже 2,7 м пересчитать до заказа каркаса	л. 73, 74 — План потолков л. 19, 21, 23, 28, 30, 37, 39, 41, 48, 50, 52, 54, 56, 58, 64, 65, 73, 85, 88, 100, 108, 127, 140–142 1-й этаж

						ГД-2026-010-АИ	
						Дом 331 м²	
Изм.	Кол.уч	Лист	№ док.	Подп.	Дата	Общая площадь 270,67* м² · * размеры приняты, не замерены (реестр — л. 8–10, К-1)	
Разраб.		Кырлан А.С.			04.11.26	Дизайн-проект интерьера	Стадия: РП; Лист: 8; Листов: 216
Пров.							
ГИП							
Н. контр.						**Открытые вопросы, принятые допущения и конфликты. Лист 1 из 3** М б/м	**Кырлан Александр Сергеевич**
Утв.							

Открытые вопросы, принятые допущения и конфликты. Лист 2 из 3

Сводка по реестрам координации (стартовое совещание 18.10.2026)

Открытые вопросы и принятые допущения (продолжение)

№	Формулировка	Вид	Кто решает	Если решения нет	Лист, где это проявляется
К-8	Душ Сн1 с трапом (санузел 1-го этажа): в стяжке 35 мм трап не встаёт — монтажная высота трапа ≈ 90 мм (по паспорту модели) + уклон отвода Ø50 до стояка Ст К1-1 (1,70 м × 25 мм/м = 42 мм) = 132 мм. Предложение проектировщика: душевая зона у стены Б под стояками (не на них), подиум 1190 × 900 высотой 100 мм (гидроизоляция по плите под подиумом и по подиуму, весь санузел; узел 1 на схеме разводки). Альтернативы: пол 1-го этажа по грунту или перекрытию с пирогом ≥ 132 мм по проекту АР/КР (тогда без подиума), низкий поддон на ножках.	Спорно Ждёт: документа, затем решения	Инженер ВК (вода, канализация)	трап и подиум не выполнять, пол санузла до решения не стяжать	л. 56, 57 — План выводов сантехники л. 19, 21, 23, 28, 30, 37, 39, 41, 48, 50, 52, 54, 56, 58, 64, 65, 73, 85, 88, 100, 108, 127, 140–142 1-й этаж л. 58, 59 — Схема разводки водопровода и канализации л. 19, 21, 23, 28, 30, 37, 39, 41, 48, 50, 52, 54, 56, 58, 64, 65, 73, 85, 88, 100, 108, 127, 140–142 1-й этаж л. 88, 89 — План полов л. 19, 21, 23, 28, 30, 37, 39, 41, 48, 50, 52, 54, 56, 58, 64, 65, 73, 85, 88, 100, 108, 127, 140–142 1-й этаж
К-9	Дверь Д-4 гостиной (пом. 5) на террасу, проём 2400 × 2100, остеклённая: число полотен и ширина полотна в данных не заданы (ряд полотен — до 1200 мм), толщина и класс безопасного стекла тоже. Одним полотном 2400 мм дверь при открывании на 90° задевает диван Гс2, такое полотно не изготовить. Решить: двупольная 2 × 1150 (сектор полотна 1150 до дивана не доходит), раздвижная или портальная система; стекло — закалённое или многослойное, толщина и класс — по выбору системы (передать стекольщику).	Отсутствует Ждёт: решения	Архитектор-планировщик	Д-4 остаётся проёмом без заданного полотна: дверь не заказать, зона открывания на плане мебели — по ширине проёма	л. 23, 24 — План дверей л. 19, 21, 23, 28, 30, 37, 39, 41, 48, 50, 52, 54, 56, 58, 64, 65, 73, 85, 88, 100, 108, 127, 140–142 1-й этаж л. 30, 31 — План расстановки мебели л. 19, 21, 23, 28, 30, 37, 39, 41, 48, 50, 52, 54, 56, 58, 64, 65, 73, 85, 88, 100, 108, 127, 140–142 1-й этаж
К-10	Кухня-столовая (пом. 1): мойка Кх1 и модули Кх6, Кх2 стоят под окном 1400 × 1500 стены А с низом проёма +0,900 — подоконник в уровне столешницы (+0,900). Смеситель мойки упирается в створку, открывающуюся внутрь, примыкание столешницы к откосу и подоконнику не решено. Выбрать: створка над мойкой глухая или поворотно-откидная с ограничителем, подоконник поднять (низ проёма от +1,050) или столешница заходит в проём вместо подоконника.	Решение Ждёт: решения	Дизайнер интерьера	столешница у окна не раскраивается, мойка Кх1 и смеситель не заказываются; монтажная схема кухни показывает проём и конфликт	л. 120 — Кухня (пом. 1). Монтажная схема
К-11	Тип котла (газ / электро / твёрдое топливо) и его мощность не выбраны. От них зависят воздухообмен и приток котельной (пом. 4; при газе — СП 62.13330, дымоход), вытяжка гаража (пом. 10) наружу своим каналом и разводка отопления от коллектора. Выбрать котёл.	Решение	Инженер ОВ	котельная и гараж без устройств вентиляции; разводка отопления — принципиальная	л. 54, 55 — План отопления л. 19, 21, 23, 28, 30, 37, 39, 41, 48, 50, 52, 54, 56, 58, 64, 65, 73, 85, 88, 100, 108, 127, 140–142 1-й этаж л. 52, 53 — План вентиляции л. 19, 21, 23, 28, 30, 37, 39, 41, 48, 50, 52, 54, 56, 58, 64, 65, 73, 85, 88, 100, 108, 127, 140–142 1-й этаж
К-12	Вентканалы ВК-1…ВК-3 приняты проектировщиком (на картинке заказчика не показаны). У санузла мансарды (пом. 20) канала нет: вытяжка ВР4 — воздуховодом ≈ 6 м до ВК-3. Нужен канал или шахта у санузла (проект дома / решение) либо подтверждение воздуховода с вентилятором по напору.	Отсутствует Ждёт: обмера	Инженер ОВ	вытяжка санузла мансарды — вентилятором с обратным клапаном и воздуховодом под потолком до ВК-3	л. 52, 53 — План вентиляции л. 19, 21, 23, 28, 30, 37, 39, 41, 48, 50, 52, 54, 56, 58, 64, 65, 73, 85, 88, 100, 108, 127, 140–142 1-й этаж
К-13	Веранда (пом. 11) и крыльцо (пом. 12): чистый пол −0,030, пирог 140 мм (утеплитель XPS 100, сборное основание ГВЛВ 25, клей 5, керамогранит 10) — верх плиты принят −0,170, то есть своя плита на 106 мм ниже плиты дома (−0,064). Отметка и конструкция плиты веранды и крыльца не известны: проект КР не передан (К-5). Подтвердить по проекту КР или обмером; если плита в уровне дома — пирог свести к 34 мм.	Отсутствует Ждёт: обмера	Архитектор-планировщик	плита веранды и крыльца — на отметке −0,170 (по пирогу); утеплитель и основание не заказывать до подтверждения отметки	л. 88, 89 — План полов л. 19, 21, 23, 28, 30, 37, 39, 41, 48, 50, 52, 54, 56, 58, 64, 65, 73, 85, 88, 100, 108, 127, 140–142 1-й этаж л. 19, 20 — Обмерный план л. 19, 21, 23, 28, 30, 37, 39, 41, 48, 50, 52, 54, 56, 58, 64, 65, 73, 85, 88, 100, 108, 127, 140–142 1-й этаж

Изм.	Кол.уч	Лист	№ док.	Подп.	Дата	ГД-2026-010-АИ			
						Дом 331 м² Общая площадь 270,67* м² · * размеры приняты, не замерены (реестр — л. 8–10, К-1)			
Разраб.		Кырлан А.С.			04.11.26	Дизайн-проект интерьера	Стадия	Лист	Листов
Пров.							РП	9	216
ГИП									
Н. контр.						Открытые вопросы, принятые допущения и конфликты. Лист 2 из 3 М б/м	Кырлан Александр Сергеевич		
Утв.									

выпуск 04.11.2026 № 2a77323a49 · стр. 9 из 221

Открытые вопросы, принятые допущения и конфликты. Лист 3 из 3

Сводка по реестрам координации (стартовое совещание 18.10.2026)

Конфликты между разделами

№	Формулировка	Разделы	Статус	Кто решает	Если решения нет	Лист, где это проявляется
Кф-1	Кухня-столовая (пом. 1): радиатор РО-1 под окном стены А (800…2200, выведен листом ОВ по оси окна) попадает в объём нижних модулей Кх6 (300…1100), Кх1 (мойка, 1100…1900) и Кх2 (посудомоечная, 1900…2500) — те же модули, что в К-10 (подоконник в уровне столешницы). Экран в модуле невозможен. Решение ОВ: перенос прибора на свободную стену (Г, у окна 1200…2800) или внутрипольный конвектор у окна; либо дизайнер меняет состав ряда у окна. Решение исполнителя (ИЗ-2, 02.11.2026, на утверждение автора): РО-1 перенесён на свободный участок стены Г у угла со стеной В (привязка 3500, 600 × 600, низ +120); ряд под окном А без прибора. Конфликт закрывается подписью ИЗ-2.	ОВ; мебель	У владельца раздела, круг 3	Инженер ОВ	до подписи ИЗ-2 модули Кх6, Кх1, Кх2 и подводки к РО-1 не выполнять	л. 54, 55 — План отопления л. 19, 21, 23, 28, 30, 37, 39, 41, 48, 50, 52, 54, 56, 58, 64, 65, 73, 85, 88, 100, 108, 127, 140–142 — 1-й этаж л. 124 — Ведомости изделий, техники и фурнитуры л. 30, 31 — План расстановки мебели л. 19, 21, 23, 28, 30, 37, 39, 41, 48, 50, 52, 54, 56, 58, 64, 65, 73, 85, 88, 100, 108, 127, 140–142 — 1-й этаж

Изменения проекта после выпуска листов (реестр изменений)

№	Дата	Лист	Было	Стало	Кто решил, подпись
ИЗ-1	30.10.2026	л. 41, 42 — План выключателей и схема включения л. 19, 21, 23, 28, 30, 37, 39, 41, 48, 50, 52, 54, 56, 58, 64, 65, 73, 85, 88, 100, 108, 127, 140–142 — 1-й этаж л. 39, 40 — План освещения л. 19, 21, 23, 28, 30, 37, 39, 41, 48, 50, 52, 54, 56, 58, 64, 65, 73, 85, 88, 100, 108, 127, 140–142 — 1-й этаж	Линия L17 объединяла светильники веранды (Св59), крыльца (Св60) и санузла 2 мансарды (Св50, Св51, вентилятор В5); единственный выключатель S9 стоял в кухне-столовой; бра Св52 (L18) без выключателя (прим. 8 «назначить управление до монтажа»).	Веранда — линия L12, выключатель S30 в гостиной у двери Д-4; крыльцо — линия L13, выключатель S31 в тамбуре у входной двери; санузел 2 — L17 (свет и вентилятор) и L18 (бра), двухклавишный S32 в холле мансарды у двери Д-13. S9 снят. Конфликт радиатора РО-1 с модулями кухни под окном записан как Кф-1.	Не утверждено: подписи нет. решение исполнителя; на утверждение А. С. Кырлана
ИЗ-2	02.11.2026	л. 54, 55 — План отопления л. 19, 21, 23, 28, 30, 37, 39, 41, 48, 50, 52, 54, 56, 58, 64, 65, 73, 85, 88, 100, 108, 127, 140–142 — 1-й этаж л. 124 — Ведомости изделий, техники и фурнитуры л. 30, 31 — План расстановки мебели л. 19, 21, 23, 28, 30, 37, 39, 41, 48, 50, 52, 54, 56, 58, 64, 65, 73, 85, 88, 100, 108, 127, 140–142 — 1-й этаж	Радиатор РО-1 выводился листом ОВ под окном стены А кухни-столовой (привязка 1050, 900 × 600) — внутри нижних модулей Кх6 (ящики), Кх1 (мойка) и Кх2 (посудомоечная машина): экран невозможен. Радиаторы дома в данных не были заданы, лист ОВ выводил их сам.	РО-1 — на свободном участке наружной стены Г у угла со стеной В: привязка 3500, 600 × 600, низ +120; ряд под окном А без прибора. Мощность РО-1 + РО-2 сверить теплотехническим расчётом ОВ (котёл и мощность не выбраны, К-11). Все радиаторы дома теперь в данных — одни и те же на листе ОВ, в мебели, DXF и IFC.	Не утверждено: подписи нет. решение исполнителя (ОВ); предложение проектировщика, на утверждение А. С. Кырлана

Примечания

1. Номера листов — по ведомости рабочих чертежей комплекта (лист «Общие данные»).
2. Графа «Если решения нет» показывает состояние решения на листах; влияние на сроки и стоимость по пунктам не оценивалось.
3. Пункт, по которому принято решение, при следующем выпуске комплекта из таблиц исключается.

Изм.	Кол.уч	Лист	№ док.	Подп.	Дата			
Разраб.		Кырлан А.С.			04.11.26	ГД-2026-010-АИ		
Пров.						Дом 331 м² Общая площадь 270,67* м² · * размеры приняты, не замерены (реестр — л. 8–10, К-1)		
ГИП						Дизайн-проект интерьера	Стадия: РП	Лист: 10 / Листов: 216
Н. контр.						**Открытые вопросы, принятые допущения и конфликты. Лист 3 из 3** М б/м	**Кырлан Александр Сергеевич**	
Утв.								

Задание на контрольный обмер и обследование. Лист 1 из 4

ПРЕДВАРИТЕЛЬНО · не для производства работ · открыто пунктов: 15 (реестр — л. 8–10)

Что замерить, вскрыть и получить до заказа материалов и изделий

Задание собрано из открытых вопросов, ответ на которые лежит на объекте или в документах, а не за столом проектировщика. Пока факт не получен, размер, материал или положение на листах — допущение (знак «*»), а не замер.
Сводка: на объекте — 11 (до демонтажа — 9; после демонтажа — 2); документом и при закупке — 5; из допущений в данных и на листах — 10, из них без вопроса в реестре — 5. Закрываются вопросы: К-1, К-2, К-4–К-8, К-12, К-13 (9). Вопросы, ждущие решения человека, задание не закрывает — они решаются по реестру открытых вопросов.

Условия проведения

Порядок работ	Приёмы и точность	Кто присутствует	Если факт не совпал с проектом
1. До демонтажа — существующее состояние: контур, диагонали, высоты, проёмы, оси стояков, ниши и конструкции, которые видны. 2. После демонтажа, до черновых работ — то, что закрывали отделка и короба: основание стен, фактические толщины, углы, узлы. 3. Документы и данные закупки — не на объекте: к сроку из последней таблицы, от них зависят привязки и заказ. Что заказывается по размеру из задания, до закрытия пункта не заказывают: сроки изготовления — по графику закупок прораба.	Обход по часовой стрелке от входа: стены, проёмы, потолок, коммуникации (стояки, щиток, вентканалы), особенности (ниши, короба, выступы). Размеры записывают в мм; сумма участков равна общему размеру, при цепочке длиннее трёх участков ставят проверочный (общий) размер. Диагонали каждого помещения; если две диагонали различаются на 5 мм и больше, разницу подписывают на плане. Потолок — в нескольких точках: центр, углы, у проёмов. Проём — ширина, высота, глубина откоса, привязка к ближайшим углам, высота подоконника. Допустимая погрешность прибора — 2–3 мм на метр; размеры округляют кратно 5 мм; два контрольных промера одного размера не должны расходиться более чем на 2 %. Допуск по пункту — в графе «Точность». План БТИ обмер не заменяет.	Прораб (отвечает за проведение) — назначает день и порядок обхода, открывает объект и освобождает помещения, ведёт это задание и реестр изменений. Архитектор — выполняет обмер, составляет акт контрольного обмера и подписывает результаты по размерам и конструкциям. Владельцы вопросов присутствуют при пунктах своего раздела или принимают результат до заказа: Инженер ВК (вода, канализация) — К-8; позиции О-1; Инженер ОВ — К-12; позиции О-3; Инженер-электрик — К-4; позиции О-2; Отделочник — позиции О-10, О-11. Заказчик или его представитель — передаёт документы (план БТИ, проект дома, технические условия, паспорта), подписывает акт. Проектных решений на обмере не принимают: обмер даёт факт, решения — по реестру открытых вопросов (листы 8–10).	1. В пределах допуска пункта — принимается измеренное значение, лист перевыпускается, знак «*» снимается. 2. Больше допуска или контрольные промеры расходятся более чем на 2 % — промер повторяют; не подтвердилось — запись в реестр изменений (дата, лист, было, стало, кто решил, подпись), работы в этом месте не начинают. 3. Затронуты несущая стена, стояк, вентканал или мокрая зона — сразу владельцу раздела и ГИПу (главному инженеру проекта); между разделами не больше двух кругов, затем решает ГИП. 4. На объекте устно ничего не согласуется: каждое решение — записью в реестр с подписью.

Этап 1. До демонтажа

№	Где	Способ	Что сделать	Кто выполняет	Точность	Что пересчитается в альбоме	Чем подтверждается	Закрывает вопросы реестра
О-1	Ввод В1 и Т3 у стояков; по всей квартире	Обмер	Отключающая арматура и счётчики воды на вводах: положение, тип, пломбы управляющей компании. Альбом ставит их на каждом вводе по практике, в данных их нет.	Архитектор	±5 мм	Узлы ввода в спецификации ВК (краны, фильтры, счётчики); места ввода на плане выводов. Листы: л. 56, 57 — План выводов сантехники л. 70 — Спецификация сантехнического оборудования	акт контрольного обмера; фото с рулеткой и привязкой к стене или углу	Вопроса в реестре нет: Альбом принимает счётчики воды на вводах без осмотра. Результат принимает: Инженер ВК (вода, канализация)
О-2	Вход в квартиру или лестничная клетка; место щита на плане	Обмер	Существующий щиток и счётчик электроэнергии: место и габарит ниши, состояние ввода, марка и сечение вводного кабеля, наличие вводного автомата и УЗО, пломбы.	Архитектор	±5 мм	Ниша и место щита на листах; вводной кабель и аппараты на однолинейной схеме; расстояния до первых групп. Листы: л. 46, 47 — Однолинейная схема щита	акт контрольного обмера; фото с рулеткой и привязкой к стене или углу	Вопроса в реестре нет: Альбом принимает щит и ввод без осмотра. Результат принимает: Инженер-электрик
О-3	у окон	Обмер	Положение стояков отопления (подающий и обратный) от граней стен, диаметры, наличие запорной арматуры; существующие радиаторы: число секций, межосевое расстояние, подводки. В данных стояков отопления нет — лист отопления выводит их условно у откоса окна.	Архитектор	±5 мм	План отопления: места стояков и подводок, привязки радиаторов; подбор радиаторов по теплотехническому расчёту; радиаторы и узлы подключения в ВОР и спецификации. Листы: л. 54, 55 — План отопления	акт контрольного обмера; фото с рулеткой и привязкой к стене или углу	Вопроса в реестре нет: Альбом принимает положение стояков и радиаторов отопления без обмера. Результат принимает: Инженер ОВ
О-4	все помещения	Обмер	Контрольный обмер всех помещений: стороны, диагонали, проёмы, высота потолка.	исполнитель	±5 мм; диагонали — разница от 5 мм подписывается	обмерный и монтажный планы, развёртки, мебель на заказ Листы: л. 19, 20 — Обмерный план л. 19, 21, 23, 28, 30, 37, 39, 41, 48, 50, 52, 54, 56, 58, 64, 65, 73, 85, 88, 100, 108, 127, 140–142 — 1-й этаж л. 30, 31 — План расстановки мебели	акт контрольного обмера	К-1 Результат принимает: Архитектор

Допущения и предложения на листе
Основа листа: размеры и контуры этажей подобраны проектировщиком по составу помещений и площадям этажей с картинки 470 px (размеры на ней не читаются); обмер и исходный проект — задание (К-1); высоты: 1-й этаж 2800 мм, мансарда 2700 мм (горизонтальная часть) приняты; скаты кровли мансарды приняты по картинке: колено 1200 мм, уклон 45°, конёк вдоль длинной стороны; проект КР — задание (К-2); наружные стены 400 мм, перегородки 120 мм приняты (К-1); разрешённая мощность 15 кВт принята по типовым ТУ для частного дома (К-4); подрайон климата не задан — принят не северный (жилые от 2,5 м) (К-7).
См. лист открытых вопросов (лист 8, записи К-1, К-2, К-4, К-7).

Изм.	Кол.уч	Лист	№ док.	Подп.	Дата
Разраб.		Кырлан А.С.			04.11.26
Пров.					
ГИП					
Н. контр.					
Утв.					

ГД-2026-010-АИ

Дом 331 м²

Общая площадь 270,67* м² · * размеры приняты, не замерены (реестр — л. 8–10, К-1)

Дизайн-проект интерьера

Стадия	Лист	Листов
РП	11	216

Задание на контрольный обмер и обследование.
Лист 1 из 4
М б/м

Кырлан Александр Сергеевич

выпуск 04.11.2026 № 2a77323a49 · стр. 11 из 221

Задание на контрольный обмер и обследование. Лист 2 из 4

Что замерить, вскрыть и получить до заказа материалов и изделий

Этап 1. До демонтажа (продолжение)

№	Где	Способ	Что сделать	Кто выполняет	Точность	Что пересчитается в альбоме	Чем подтверждается	Закрывает вопросы реестра
О-5	Все помещения квартиры	Обмер	Высота потолка в каждом помещении в нескольких точках: центр, углы, у проёмов.	Архитектор	±5 мм	Вертикальные размеры альбома: развёртки, шкафы, плитка, объёмы работ. Листы: л. 2–7 — Общие данные	акт контрольного обмера	К-2 Результат принимает: Архитектор
О-6	холл с лестницей / холл мансарды	Обмер	Разность отметок чистых полов 1-го этажа и мансарды, толщина перекрытия, положение и размеры проёма над маршем (по проекту КР или по факту).	исполнитель		лист «Лестница Л-1*», планы этажей, ведомость ограждений Листы: architect/stairs-л-1 (лист по названию не найден)		К-6 Результат принимает: Архитектор
О-7	По месту	Обмер	Подтвердить на объекте принятое: подрайон климата не задан — принят не северный (жилые от 2,5 м)	Архитектор	±5 мм	Листы, где используется принятая величина. Листы: л. 2–7 — Общие данные	акт контрольного обмера	К-7 Результат принимает: Архитектор
О-8	санузел, ванная, кухня	Обмер	Положение и сечение вентканалов (вентблока), тяга.	исполнитель	±10 мм	план вентиляции, потолки, короба Листы: л. 52, 53 — План вентиляции л. 19, 21, 23, 28, 30, 37, 39, 41, 48, 50, 52, 54, 56, 58, 64, 65, 73, 85, 88, 100, 108, 127, 140–142 — 1-й этаж	акт контрольного обмера	К-12 Результат принимает: Инженер ОВ
О-9	веранда (пом. 11), крыльцо (пом. 12)	Обмер	Отметка верха плиты веранды и крыльца от ±0,000 дома (нивелиром), конструкция плиты.	исполнитель	±5 мм	экспликация полов, ведомость объёмов Листы: л. 88, 89 — План полов л. 19, 21, 23, 28, 30, 37, 39, 41, 48, 50, 52, 54, 56, 58, 64, 65, 73, 85, 88, 100, 108, 127, 140–142 — 1-й этаж л. 19, 20 — Обмерный план	акт контрольного обмера	К-13 Результат принимает: Архитектор

Допущения и предложения на листе

Основа листа: размеры и контуры этажей подобраны проектировщиком по составу помещений и площадям этажей с картинки 470 px (размеры на ней не читаются); обмер и исходный проект — задание (К-1); высоты: 1-й этаж 2800 мм, мансарда 2700 мм (горизонтальная часть) приняты; скаты кровли мансарды приняты по картинке: колено 1200 мм, уклон 45°, конёк вдоль длинной стороны; проект КР — задание (К-2); наружные стены 400 мм, перегородки 120 мм приняты (К-1); разрешённая мощность 15 кВт принята по типовым ТУ для частного дома (К-4); подрайон климата не задан — принят не северный (жилые от 2,5 м) (К-7).

Знак «*» — принято, не замерено и не подтверждено (замерить на объекте): К-6: Л-1 — габарит марша снят с картинки заказчика (11 проступей в холле 3,6 м), а до отм. +3,150 нужно 18 подъёмов — одномаршевая не встаёт: решение по К-6.

См. лист открытых вопросов (лист 8, записи К-1, К-2, К-4, К-6, К-7).

Изм.	Кол.уч	Лист	№ док.	Подп.	Дата
Разраб.		Кырлан А.С.			04.11.26
Пров.					
ГИП					
Н. контр.					
Утв.					

ГД-2026-010-АИ

Дом 331 м²

Общая площадь 270,67* м² · * размеры приняты, не замерены (реестр — л. 8–10, К-1)

Дизайн-проект интерьера

Стадия	Лист	Листов
РП	12	216

Задание на контрольный обмер и обследование.
Лист 2 из 4
М б/м

Кырлан Александр Сергеевич

выпуск 04.11.2026 № 2a77323a49 · стр. 12 из 221

Задание на контрольный обмер и обследование. Лист 3 из 4

ПРЕДВАРИТЕЛЬНО · не для производства работ · открыто пунктов: 15 (реестр — л. 8–10)

Что замерить, вскрыть и получить до заказа материалов и изделий

Этап 2. После демонтажа, до черновых работ

№	Где	Способ	Что сделать	Кто выполняет	Точность	Что пересчитается в альбоме	Чем подтверждается	Закрывает вопросы реестра
О-10	Кухня-столовая (пом. 1), Кабинет-гостевая (пом. 2), Санузел 1 этажа (пом. 3), Котельная (пом. 4), Гостиная (пом. 5), Холл с лестницей (пом. 6), Кладовая (пом. 7), Прихожая (пом. 8), Тамбур (пом. 9), Гараж (пом. 10), Веранда (пом. 11), Крыльцо (пом. 12), Спальня мастер (пом. 13), Гардеробная мастер (пом. 14), Санузел мастер (пом. 15), Спальня 2 (пом. 16), Холл мансарды (пом. 17), Спальня 3 (пом. 18), Спальня 4 (пом. 19), Санузел 2 (пом. 20)	Обмер	Нивелировка плиты перекрытия и существующего пола после демонтажа покрытий: отметки в углах и по сетке, перепады по помещению, уклоны, отметки порогов (чистый пол в мокрых зонах принят -30 мм, -15 мм, 0 мм). Принятая толщина стяжки 33 мм, 47 мм, 49 мм, 50 мм, 61 мм и отметка чистого пола расчётные, не от замера плиты.	Архитектор	±5 мм по отметке; ровность просвет под 2-метровой рейкой, горизонталь против 0,2 % длины помещения	Толщина стяжки и отметка чистого пола; уклоны к трапам и пороги; выпуски К1 относительно чистого пола (план разводки); объёмы стяжки и смеси в ВОР и спецификации. Листы: л. 82, 88–90 — План полов л. 58, 59 — Схема разводки водопровода и канализации	акт контрольного обмера	Вопроса в реестре нет: Альбом принимает отметки плиты и толщину пирога пола без нивелировки. Результат принимает: Отделочник
О-11	Кухня-столовая (пом. 1), Кабинет-гостевая (пом. 2), Санузел 1 этажа (пом. 3), Котельная (пом. 4), Гостиная (пом. 5), Холл с лестницей (пом. 6), Кладовая (пом. 7), Прихожая (пом. 8), Тамбур (пом. 9), Гараж (пом. 10), Веранда (пом. 11), Крыльцо (пом. 12), Спальня мастер (пом. 13), Гардеробная мастер (пом. 14), Санузел мастер (пом. 15), Спальня 2 (пом. 16), Холл мансарды (пом. 17), Спальня 3 (пом. 18), Спальня 4 (пом. 19), Санузел 2 (пом. 20)	Обмер	Вертикаль и плоскостность стен: отклонение от вертикали по высоте стены (отвес или лазерный уровень), просвет под правилом 2 м, кривизна углов. Нужно там, где от стены зависит изделие: облицовка плиткой (пом. 3, 15, 20), штукатурка и окраска (пом. 1, 2, 3, 4, 5, 6, 7, 8, 9, 10, 11, 12, 13, 14, 15, 16, 17, 18, 19, 20), встроенная мебель и кухня (пом. 1, 8, 16, 18, 19).	Архитектор	до 1 мм на 2 м (правило и клиновой щуп); вертикаль — мм на высоту стены, отклонения подписываются на плане	Толщина штукатурки и расход смеси в ВОР и спецификации; раскладка плитки (подрезка у стен); зазоры и крепление встроенной мебели и кухни. Листы: л. 82–87 — Раскладка плитки л. 91–94 — Ведомость отделки помещений	акт контрольного обмера	Вопроса в реестре нет: Альбом принимает стены ровными и вертикальными без замера. Результат принимает: Отделочник

Документы и данные закупки (не на объекте)

№	У кого, откуда	Способ	Что получить	К какому сроку	Что пересчитается в альбоме	Чем подтверждается	Закрывает вопросы реестра
О-12	Заказчик; организация, выдавшая технические условия	Документ	Технические условия на присоединение: разрешённая мощность.	До утверждения однолинейной схемы щита	Однолинейная схема щита: вводной аппарат и группы. Листы: л. 2–7 — Общие данные	копия документа	К-4 Результат принимает: Инженер-электрик
О-13	вся квартира	Документ	Поэтажный план БТИ и техническое заключение о несущих стенах.	до демонтажа и возведения перегородок	монтажный план, проёмы, развёртки Листы: л. 19, 20 — Обмерный план л. 19, 21, 23, 28, 30, 37, 39, 41, 48, 50, 52, 54, 56, 58, 64, 65, 73, 85, 88, 100, 108, 127, 140–142 — 1-й этаж	копия документа	К-5 Результат принимает: Архитектор

Допущения и предложения на листе

Основа листа: размеры и контуры этажей подобраны проектировщиком по составу помещений и площадям этажей с картинки 470 px (размеры на ней не читаются); обмер и исходный проект — задание (К-1); высоты: 1-й этаж 2800 мм, мансарда 2700 мм (горизонтальная часть) приняты; скаты кровли мансарды приняты по картинке: колено 1200 мм, уклон 45°, конёк вдоль длинной стороны; проект КР — задание (К-2); наружные стены 400 мм, перегородки 120 мм приняты (К-1); разрешённая мощность 15 кВт принята по типовым ТУ для частного дома (К-4); подрайон климата не задан — принят не северный (жилые от 2,5 м) (К-7).

См. лист открытых вопросов (лист 8, записи К-1, К-2, К-4, К-7).

Изм.	Кол.уч	Лист	№ док.	Подп.	Дата
Разраб.		Кырлан А.С.			04.11.26
Пров.					
ГИП					
Н. контр.					
Утв.					

ГД-2026-010-АИ

Дом 331 м²

Общая площадь 270,67* м² · * размеры приняты, не замерены (реестр — л. 8–10, К-1)

Дизайн-проект интерьера

Стадия	Лист	Листов
РП	13	216

Задание на контрольный обмер и обследование.
Лист 3 из 4
М б/м

Кырлан Александр Сергеевич

выпуск 04.11.2026 № 2a77323a49 · стр. 13 из 221

Задание на контрольный обмер и обследование. Лист 4 из 4

Что замерить, вскрыть и получить до заказа материалов и изделий

Документы и данные закупки (не на объекте) (продолжение)

№	У кого, откуда	Способ	Что получить	К какому сроку	Что пересчитается в альбоме	Чем подтверждается	Закрывает вопросы реестра
О-14	адрес объекта, СП 131.13330	Документ	Климатический подрайон по СП 131.13330 (по адресу объекта)	до заказа каркаса потолков	план потолков, разрезы, ведомость объёмов Листы: л. 73, 74 — План потолков л. 19, 21, 23, 28, 30, 37, 39, 41, 48, 50, 52, 54, 56, 58, 64, 65, 73, 85, 88, 100, 108, 127, 140–142 — 1-й этаж	копия документа	К-7 Результат принимает: Архитектор
О-15	санузел 1-го этажа	Документ	Конструкция пола 1-го этажа (по грунту / по перекрытию) и отметка врезки в стояк Ст К1-1.	до черновой разводки канализации и стяжки	высота подиума, профиль К1 (схема разводки) Листы: л. 56, 57 — План выводов сантехники л. 19, 21, 23, 28, 30, 37, 39, 41, 48, 50, 52, 54, 56, 58, 64, 65, 73, 85, 88, 100, 108, 127, 140–142 — 1-й этаж л. 58, 59 — Схема разводки водопровода и канализации л. 88, 89 — План полов	копия документа	К-8 Результат принимает: Инженер ВК (вода, канализация)
О-16	Поставщик изделий; Веранда (пом. 11), Крыльцо (пом. 12)	Закупка	Паспорт или монтажная схема выбранной модели: пол пом. 11 (atlas concorde marvel travertine a8uz) — габариты, положение и выводы (вода, слив, электро) по паспорту выбранной модели, пол пом. 12 (atlas concorde marvel travertine a8uz) — габариты, положение и выводы (вода, слив, электро) по паспорту выбранной модели. Принято в проекте: отметка верха плиты −0,170 принята по пирогу (плита веранды и крыльца своя, ниже плиты дома) подтвердить по проекту КР или обмером (К-13).	До закрытия трасс и разводки	Габариты и положение изделий на планах и развёртках, выводы (вода, слив, электро), монтажные зазоры; знак «*» у марки снимается паспортом или чертежом. Листы: л. 30, 31 — План расстановки мебели	паспорт изделия или партии	К-13 Результат принимает: Архитектор

Примечания

1. Подтверждение: акт контрольного обмера (дата, кто присутствовал, прибор, перечень промеров с результатами, подписи присутствующих); к акту — фото вскрытий и узлов и техническое заключение организации, выполнившей обследование.
2. Номера листов — по ведомости рабочих чертежей комплекта (лист «Общие данные»).
3. Пункт исключается из задания при следующем выпуске, когда акт подписан, значение внесено в проект и листы перевыпущены; знак «*» у величины снимается только замером.

Допущения и предложения на листе

Основа листа: размеры и контуры этажей подобраны проектировщиком по составу помещений и площадям этажей с картинки 470 px (размеры на ней не читаются); обмер и исходный проект — задание (К-1); высоты: 1-й этаж 2800 мм, мансарда 2700 мм (горизонтальная часть) приняты; скаты кровли мансарды приняты по картинке: колено 1200 мм, уклон 45°, конёк вдоль длинной стороны; проект КР — задание (К-2); наружные стены 400 мм, перегородки 120 мм приняты (К-1); разрешённая мощность 15 кВт принята по типовым ТУ для частного дома (К-4); подрайон климата не задан — принят не северный (жилые от 2,5 м) (К-7).
См. лист открытых вопросов (лист 8, записи К-1, К-2, К-4, К-7).

Изм.	Кол.уч	Лист	№ док.	Подп.	Дата
Разраб.		Кырлан А.С.			04.11.26
Пров.					
ГИП					
Н. контр.					
Утв.					

ГД-2026-010-АИ

Дом 331 м²

Общая площадь 270,67* м² · * размеры приняты, не замерены (реестр — л. 8–10, К-1)

Дизайн-проект интерьера

Стадия	Лист	Листов
РП	14	216

Задание на контрольный обмер и обследование.
Лист 4 из 4
М б/м

Кырлан Александр Сергеевич

выпуск 04.11.2026 № 2a77323a49 · стр. 14 из 221

ПРЕДВАРИТЕЛЬНО · не для производства работ · открыто пунктов: 15 (реестр — л. 8–10)

График закупок и работ. Лист 1 из 4

Что заказывать и когда не раньше чего: относительный порядок без дат; срок поставки — из данных или «не задан» с записью реестра

Лист не содержит дат: контрольного обмера, подписанных решений автора и договоров ещё нет, и любая дата была бы выдумана. Вместо календаря — порядок и условия: замер → решение и выбор изделия → заказ → срок поставки → работа, которую позиция блокирует.
Срок поставки печатается как срок, только если он задан в данных позиции. Нет — «срок поставки не задан» и ссылка на вопрос реестра о сроках; типовой диапазон практики стоит рядом как ориентир и заказывать по нему нельзя. Номера З-N и Р-N — строки этого листа, К-N — записи реестра открытых вопросов, О-N — позиции задания на контрольный обмер.

Закупки: что заказывается, от чего зависит заказ и какую работу блокирует

№	Позиция и где	1. Замер до заказа	2. Решение, выбор изделия, паспорт	3. Условие заказа	4. Срок поставки	5. Блокирует работу	Закрывает вопросы реестра
З-1	Двери скрытого монтажа с коробом под покраску в существующих проёмах: Д-1, Д-2, Д-7, Д-8, Д-9, Д-10, Д-11, Д-12, Д-13 — 9 шт. пом. 2, 3, 13, 14, 15, 16, 18, 19, 20	О-4: обмер: все помещения (К-1); до заказа мебели и дверей		После 1 и 2 и после получения срока у поставщика (вопроса о сроках нет); дата заказа — когда срок известен, не позднее чем за срок до начала Р-5.	срок поставки не задан (записи реестра нет) Ориентир практики (не срок поставщика): ≈ 30 дн.	Р-5 «штукатурка»: короб ставят до штукатурки (коробку ставят на черновой стадии; полотно навешивают после чистовой отделки стен)	К-1
З-2	Кухонный гарнитур по проекту кухни: модули Кх1, Кх2, Кх4, Кх3, Кх5, Кх6, Кх10, Кх11, Кх12, Кх13 пом. 1			После 1 и 2 и после получения срока у поставщика (вопроса о сроках нет); дата заказа — когда срок известен, не позднее чем за срок до начала Р-15.	срок поставки не задан (записи реестра нет) Ориентир практики (не срок поставщика): 4–8 нед. от замера	Р-15 «кухня и мебель»: замер кухни — по готовым стенам после штукатурки или плитки, до чистового пола; производство идёт параллельно со стяжкой и отделкой	
З-3	Встраиваемая техника кухни: Кх2 посудомоечная машина, Кх5 холодильник пом. 1			После 1 и 2 и после получения срока у поставщика (вопроса о сроках нет); дата заказа — когда срок известен, не позднее чем за срок до начала Р-15.	срок поставки не задан (записи реестра нет)	Р-15 «кухня и мебель»: паспорта и монтажные схемы — до изготовления модулей кухни: нишу и вентзазоры задаёт модель, а не типовая схема 60 см	
З-4	Стиральная машина: Сд4 (вертикальная загрузка 400 × 600 мм — условие закупки) пом. 20			После 1 и 2 и после получения срока у поставщика (вопроса о сроках нет); дата заказа — когда срок известен, не позднее чем за срок до начала Р-4.	срок поставки не задан (записи реестра нет)	Р-4 «черновая сантехника»: габарит и подводка — до закрытия люка и разводки	
З-5	Сантехнические приборы и инсталляции: Сн1**, Сн2, Сн3, См1, См2, См3, Сд1, Сд2, Сд3 пом. 3, 15, 20	О-3: обмер: у окон		После 1 и 2 и после получения срока у поставщика (вопроса о сроках нет); дата заказа — когда срок известен, не позднее чем за срок до начала Р-4.	срок поставки не задан (записи реестра нет)	Р-4 «черновая сантехника»: инсталляцию ставят до обшивки ГКЛВ и до гидроизоляции стены	

Допущения и предложения на листе

Основа листа: размеры и контуры этажей подобраны проектировщиком по составу помещений и площадям этажей с картинки 470 px (размеры на ней не читаются); обмер и исходный проект — задание (К-1); высоты: 1-й этаж 2800 мм, мансарда 2700 мм (горизонтальная часть) приняты; скаты кровли мансарды приняты по картинке: колено 1200 мм, уклон 45°, конёк вдоль длинной стороны; проект КР — задание (К-2); наружные стены 400 мм, перегородки 120 мм приняты (К-1); разрешённая мощность 15 кВт принята по типовым ТУ для частного дома (К-4); подрайон климата не задан — принят не северный (жилые от 2,5 м) (К-7).
Знак «**» — предложение проектировщика, заказчиком не утверждено (согласовать с заказчиком): К-8: Сн1 — Подиум душевой зоны 100 мм — предложение проектировщика: трап в стяжке 35 мм не встаёт (монтажная высота трапа 90 + уклон отвода до стояка 42 = 132 мм).
См. лист открытых вопросов (лист 8, записи К-1, К-2, К-4, К-7; лист 9, запись К-8).

Изм.	Кол.уч	Лист	№ док.	Подп.	Дата
Разраб.		Кырлан А.С.			04.11.26
Пров.					
ГИП					
Н. контр.					
Утв.					

ГД-2026-010-АИ

Дом 331 м²

Общая площадь 270,67* м² · * размеры приняты, не замерены (реестр — л. 8–10, К-1)

Дизайн-проект интерьера

Стадия	Лист	Листов
РП	15	216

График закупок и работ. Лист 1 из 4

М б/м

Кырлан Александр Сергеевич

выпуск 04.11.2026 № 2a77323a49 · стр. 15 из 221

График закупок и работ. Лист 2 из 4

Что заказывать и когда не раньше чего: относительный порядок без дат; срок поставки — из данных или «не задан» с записью реестра

Закупки: что заказывается, от чего зависит заказ и какую работу блокирует (продолжение)

№	Позиция и где	1. Замер до заказа	2. Решение, выбор изделия, паспорт	3. Условие заказа	4. Срок поставки	5. Блокирует работу	Закрывает вопросы реестра
З-6	Керамогранит и плитка: 2 поз. по артикулу и формату, 126,65 м² по раскладке пом. 3, 4, 8, 9, 11, 12, 15, 20	О-10: обмер: Кухня-столовая (пом. 1), Кабинет-гостевая (пом. 2), Санузел 1 этажа (пом. 3), Котельная (пом. 4), Гостиная (пом. 5), Холл с лестницей (пом. 6), Кладовая (пом. 7), Прихожая (пом. 8), Тамбур (пом. 9), Гараж (пом. 10), Веранда (пом. 11), Крыльцо (пом. 12), Спальня мастер (пом. 13), Гардеробная мастер (пом. 14), Санузел мастер (пом. 15), Спальня 2 (пом. 16), Холл мансарды (пом. 17), Спальня 3 (пом. 18), Спальня 4 (пом. 19), Санузел 2 (пом. 20) О-11: обмер: Кухня-столовая (пом. 1), Кабинет-гостевая (пом. 2), Санузел 1 этажа (пом. 3), Котельная (пом. 4), Гостиная (пом. 5), Холл с лестницей (пом. 6), Кладовая (пом. 7), Прихожая (пом. 8), Тамбур (пом. 9), Гараж (пом. 10), Веранда (пом. 11), Крыльцо (пом. 12), Спальня мастер (пом. 13), Гардеробная мастер (пом. 14), Санузел мастер (пом. 15), Спальня 2 (пом. 16), Холл мансарды (пом. 17), Спальня 3 (пом. 18), Спальня 4 (пом. 19), Санузел 2 (пом. 20)		После 1 и 2 и после получения срока у поставщика (вопроса о сроках нет); дата заказа — когда срок известен, не позднее чем за срок до начала Р-9.	срок поставки не задан (записи реестра нет)	Р-9 «плитка»: калибр партии измеряют до раскладки, раскладку пересчитывают до заказа	
З-7	Покрытие пола (доска) и плинтус: пом. 1, 2, 5, 6, 7, 13, 14, 16, 17, 18, 19 пом. 1, 2, 5, 6, 7, 13, 14, 16, 17, 18, 19	О-10: обмер: Кухня-столовая (пом. 1), Кабинет-гостевая (пом. 2), Санузел 1 этажа (пом. 3), Котельная (пом. 4), Гостиная (пом. 5), Холл с лестницей (пом. 6), Кладовая (пом. 7), Прихожая (пом. 8), Тамбур (пом. 9), Гараж (пом. 10), Веранда (пом. 11), Крыльцо (пом. 12), Спальня мастер (пом. 13), Гардеробная мастер (пом. 14), Санузел мастер (пом. 15), Спальня 2 (пом. 16), Холл мансарды (пом. 17), Спальня 3 (пом. 18), Спальня 4 (пом. 19), Санузел 2 (пом. 20)		После 1 и 2 и после получения срока у поставщика (вопроса о сроках нет); дата заказа — когда срок известен, не позднее чем за срок до начала Р-12.	срок поставки не задан (записи реестра нет)	Р-12 «чистовые полы»: артикул и партия — до заказа; доску привозят к чистовым полам	
З-8	Встроенная мебель по замеру цеха: Пх1, С3, Дт3, Дт6 пом. 8, 16, 18, 19	О-4: обмер: все помещения (К-1); до заказа мебели и дверей		После 1 и 2 и после получения срока у поставщика (вопроса о сроках нет); дата заказа — когда срок известен, не позднее чем за срок до начала Р-15.	срок поставки не задан (записи реестра нет) Ориентир практики (не срок поставщика): 4–8 нед. от замера	Р-15 «кухня и мебель»: цех замеряет по готовым стенам; производство 4–8 недель идёт параллельно с отделкой	К-1

Допущения и предложения на листе

Основа листа: размеры и контуры этажей подобраны проектировщиком по составу помещений и площадям этажей с картинки 470 px (размеры на ней не читаются); обмер и исходный проект — задание (К-1); высоты: 1-й этаж 2800 мм, мансарда 2700 мм (горизонтальная часть) приняты; скаты кровли мансарды приняты по картинке: колено 1200 мм, уклон 45°, конёк вдоль длинной стороны; проект КР — задание (К-2); наружные стены 400 мм, перегородки 120 мм приняты (К-1); разрешённая мощность 15 кВт принята по типовым ТУ для частного дома (К-4); подрайон климата не задан — принят не северный (жилые от 2,5 м) (К-7).

См. лист открытых вопросов (лист 8, записи К-1, К-2, К-4, К-7).

Изм.	Кол.уч	Лист	№ док.	Подп.	Дата
Разраб.		Кырлан А.С.			04.11.26
Пров.					
ГИП					
Н. контр.					
Утв.					

ГД-2026-010-АИ

Дом 331 м²

Общая площадь 270,67* м² · * размеры приняты, не замерены (реестр — л. 8–10, К-1)

Дизайн-проект интерьера

Стадия	Лист	Листов
РП	16	216

График закупок и работ. Лист 2 из 4

М б/м

Кырлан Александр Сергеевич

выпуск 04.11.2026 № 2a7732a49 · стр. 16 из 221

График закупок и работ. Лист 3 из 4

Что заказывать и когда не раньше чего: относительный порядок без дат; срок поставки — из данных или «не задан» с записью реестра

Работы: порядок и что не даёт начать

№	Работа (стадия технологической последовательности)	После	Что должно быть к началу: условия и закупки	Не начинать, пока открыто в реестре
Р-1	Демонтаж покрытий, отделки стен и потолков, дверных блоков и приборов; конструкции, стены и перегородки не трогать до технического заключения (стадия 1)		до начала: запрошены документы на дом и БТИ; контрольный обмер до демонтажа (что видно) сделан	
Р-2	Контрольный обмер на голых стенах и обследование (задание — лист «Задание на контрольный обмер») (стадия 2)	Р-1	после снятия отделки: видны стояки, каналы, щиток, толщины стен; до заказа всего, что делают по размеру	
Р-3	Черновая электрика: штробы, короба, гофра, подрозетники, щит (стадия 4)	Р-2	до начала: план электрики с высотами утверждён; штробы в стенах — только после технического заключения; мебель расставлена	К-4: Разрешённая мощность дома по ТУ неизвестна, принята 15 кВт.
Р-4	Черновая сантехника и вентиляция: разводка, выводы, инсталляции, короба стояков (стадия 5)	Р-2	до начала: положение стояков замерено; модели инсталляций и машины выбраны (габариты рамы, подводка); инсталляцию ставят до обшивки ГКЛВ и до гидроизоляции Закупки к началу: З-4 (стиральная машина), З-5 (сантехника)	
Р-5	Коробки скрытых дверей, затем штукатурка стен и откосов (стадия 6)	Р-2, Р-3, Р-4	до начала: электрика и сантехника смонтированы, штробы заделаны; коробки скрытых дверей установлены до штукатурки (поэтому заказ дверей — раньше работы) Закупки к началу: З-1 (двери скрытого монтажа)	К-1: Размеры дома на картинке заказчика (470 px) не читаются: состав помещений и форма сняты с картинки, размеры подобраны проектировщиком под площади этажей 185,80 и 145,73 м².
Р-6	Стяжка пола и тёплый пол (стадия 7)	Р-5	до начала: штукатурка сделана; трубы под стяжкой приняты; нивелировка плиты выполнена	
Р-7	Гидроизоляция санузлов и тест проливом (стадия 8)	Р-6	до начала: стяжка набрала прочность и сухая по инструкции гидроизоляции; выводы стоят на проектных отметках	
Р-8	ГКЛ: короба инсталляции и стояков, ниши, потолки (стадия 9)	Р-3, Р-4	до начала: черновые сети в зоне коробов приняты; закладные под тяжёлое и карнизы стоят; светильники выбраны (вырезы)	

Допущения и предложения на листе

Основа листа: размеры и контуры этажей подобраны проектировщиком по составу помещений и площадям этажей с картинки 470 px (размеры на ней не читаются); обмер и исходный проект — задание (К-1); высоты: 1-й этаж 2800 мм, мансарда 2700 мм (горизонтальная часть) приняты; скаты кровли мансарды приняты по картинке: колено 1200 мм, уклон 45°, конёк вдоль длинной стороны; проект КР — задание (К-2); наружные стены 400 мм, перегородки 120 мм приняты (К-1); разрешённая мощность 15 кВт принята по типовым ТУ для частного дома (К-4); подрайон климата не задан — принят не северный (жилые от 2,5 м) (К-7).

См. лист открытых вопросов (лист 8, записи К-1, К-2, К-4, К-7).

Изм.	Кол.уч	Лист	№ док.	Подп.	Дата
Разраб.		Кырлан А.С.			04.11.26
Пров.					
ГИП					
Н. контр.					
Утв.					

ГД-2026-010-АИ

Дом 331 м²

Общая площадь 270,67* м² · * размеры приняты, не замерены (реестр — л. 8–10, К-1)

Дизайн-проект интерьера

Стадия	Лист	Листов
РП	17	216

График закупок и работ. Лист 3 из 4

М б/м

Кырлан Александр Сергеевич

выпуск 04.11.2026 № 2a77323a49 · стр. 17 из 221

График закупок и работ. Лист 4 из 4

Что заказывать и когда не раньше чего: относительный порядок без дат; срок поставки — из данных или «не задан» с записью реестра

Работы: порядок и что не даёт начать (продолжение)

№	Работа (стадия технологической последовательности)	После	Что должно быть к началу: условия и закупки	Не начинать, пока открыто в реестре
Р-9	Плитка и керамогранит: стены, затем пол; фартук (стадия 10)	Р-6, Р-7, Р-8	до начала: гидроизоляция принята; плитка выбрана, калибр партии измерен, раскладка пересчитана и подписана Закупки к началу: З-6 (плитка)	
Р-10	Шпаклёвка стен и потолков под окраску (стадия 11)	Р-5, Р-8, Р-9	до начала: плитка готова (грязные работы закончены); штукатурка и ГКЛ сухие	
Р-11	Окраска стен, потолков, откосов (стадия 13)	Р-10	до начала: шпаклёвка отшлифована и огрунтована; выкрасы утверждены, колеровка одной партией	
Р-12	Чистовые полы: инженерная доска (стадия 14)	Р-9, Р-11	до начала: влажность основания в норме, мокрые работы закончены; доска выбрана и привезена Закупки к началу: З-7 (доска и плинтус)	
Р-13	Полотна межкомнатных дверей, плинтусы, пороги (стадия 15)	Р-11, Р-12	до начала: чистовой пол уложен; полотна скрытых дверей — после чистовой отделки стен	
Р-14	Чистовая электрика и сантехника: механизмы, светильники, смесители, приборы (стадия 16)	Р-11, Р-13	до начала: отделка готова; механизмы, светильники и приборы выбраны и привезены	
Р-15	Кухня, встроенная и корпусная мебель, бытовая техника (стадия 17)	Р-13, Р-14	до начала: чистовая сантехника и электрика подведены к местам мебели; замер кухни снят по готовым стенам (после штукатурки или плитки, до чистового пола) Закупки к началу: З-2 (кухонный гарнитур), З-3 (техника кухни), З-8 (мебель по замеру)	К-1: Размеры дома на картинке заказчика (470 px) не читаются: состав помещений и форма сняты с картинки, размеры подобраны проектировщиком под площади этажей 185,80 и 145,73 м².
Р-16	Сдача: осмотр по чек-листу, дефектная ведомость, устранение замечаний (стадия 18)	Р-14, Р-15	до начала: всё смонтировано; акты скрытых работ подписаны	

Примечания

1. Порядок работ — стадии технологической последовательности из 16 позиций, присутствующих в этом проекте (по строкам ведомости объёмов); остальные стадии таблицы knowledge/remont-tehnologiya.md в проекте не встречаются. Длительности работ не печатаются: их нет ни в данных, ни в нормах для этого объекта.
2. Типовые сроки — ориентир практики, не срок поставщика: скрытые двери — короб около 10 дн., полотно под покраску до 3 нед., шпон 4–5 нед., в среднем около 30 дн. (knowledge/workers/foreman.md, п. 2.4 (profil-doors)); кухня и корпусная мебель — 4–8 недель от замера (knowledge/remont-tehnologiya.md, разд. 2; knowledge/workers/foreman.md, п. 2.4). Заказ по ориентиру не назначается: срок получают у поставщика (вопрос реестра), после чего заказ планируют «не позднее чем за срок до начала работы».
3. Условия заказа берутся из реестра открытых вопросов и задания на контрольный обмер: позиция заказывается, когда закрыты замер (графа 1) и решение (графа 2). Закрывать их может только факт или решение автора с подписью; снять строку с листа можно только закрыв запись реестра.
4. Заказ по размеру до контрольного обмера не делают: двери, кухня и встроенная мебель зависят от обмера (К-11, К-13); скрытые двери, кроме того, зависят от решения по нише санузла 2 (проём Д-5 в перегородке П-1).
5. Номера листов — по ведомости рабочих чертежей комплекта (лист «Общие данные»).

Допущения и предложения на листе

Основа листа: размеры и контуры этажей подобраны проектировщиком по составу помещений и площадям этажей с картинки 470 px (размеры на ней не читаются); обмер и исходный проект — задание (К-1); высоты: 1-й этаж 2800 мм, мансарда 2700 мм (горизонтальная часть) приняты; скаты кровли мансарды приняты по картинке: колено 1200 мм, уклон 45°, конёк вдоль длинной стороны; проект КР — задание (К-2); наружные стены 400 мм, перегородки 120 мм приняты (К-1); разрешённая мощность 15 кВт принята по типовым ТУ для частного дома (К-4); подрайон климата не задан — принят не северный (жилые от 2,5 м) (К-7).
См. лист открытых вопросов (лист 8, записи К-1, К-2, К-4, К-7).

Изм.	Кол.уч	Лист	№ док.	Подп.	Дата
Разраб.		Кырлан А.С.			04.11.26
Пров.					
ГИП					
Н. контр.					
Утв.					

ГД-2026-010-АИ

Дом 331 м²

Общая площадь 270,67* м² · * размеры приняты, не замерены (реестр — л. 8–10, К-1)

Дизайн-проект интерьера

Стадия	Лист	Листов
РП	18	216

График закупок и работ. Лист 4 из 4

М б/м


Кырлан Александр Сергеевич

выпуск 04.11.2026 № 2a7323a49 · стр. 18 из 221

Обмерный план · 1-й этаж

Существующее положение · размеры в мм · отметки от чистого пола

ПРЕДВАРИТЕЛЬНО · не для производства работ · открыто пунктов: 15 (реестр — л. 8–10)

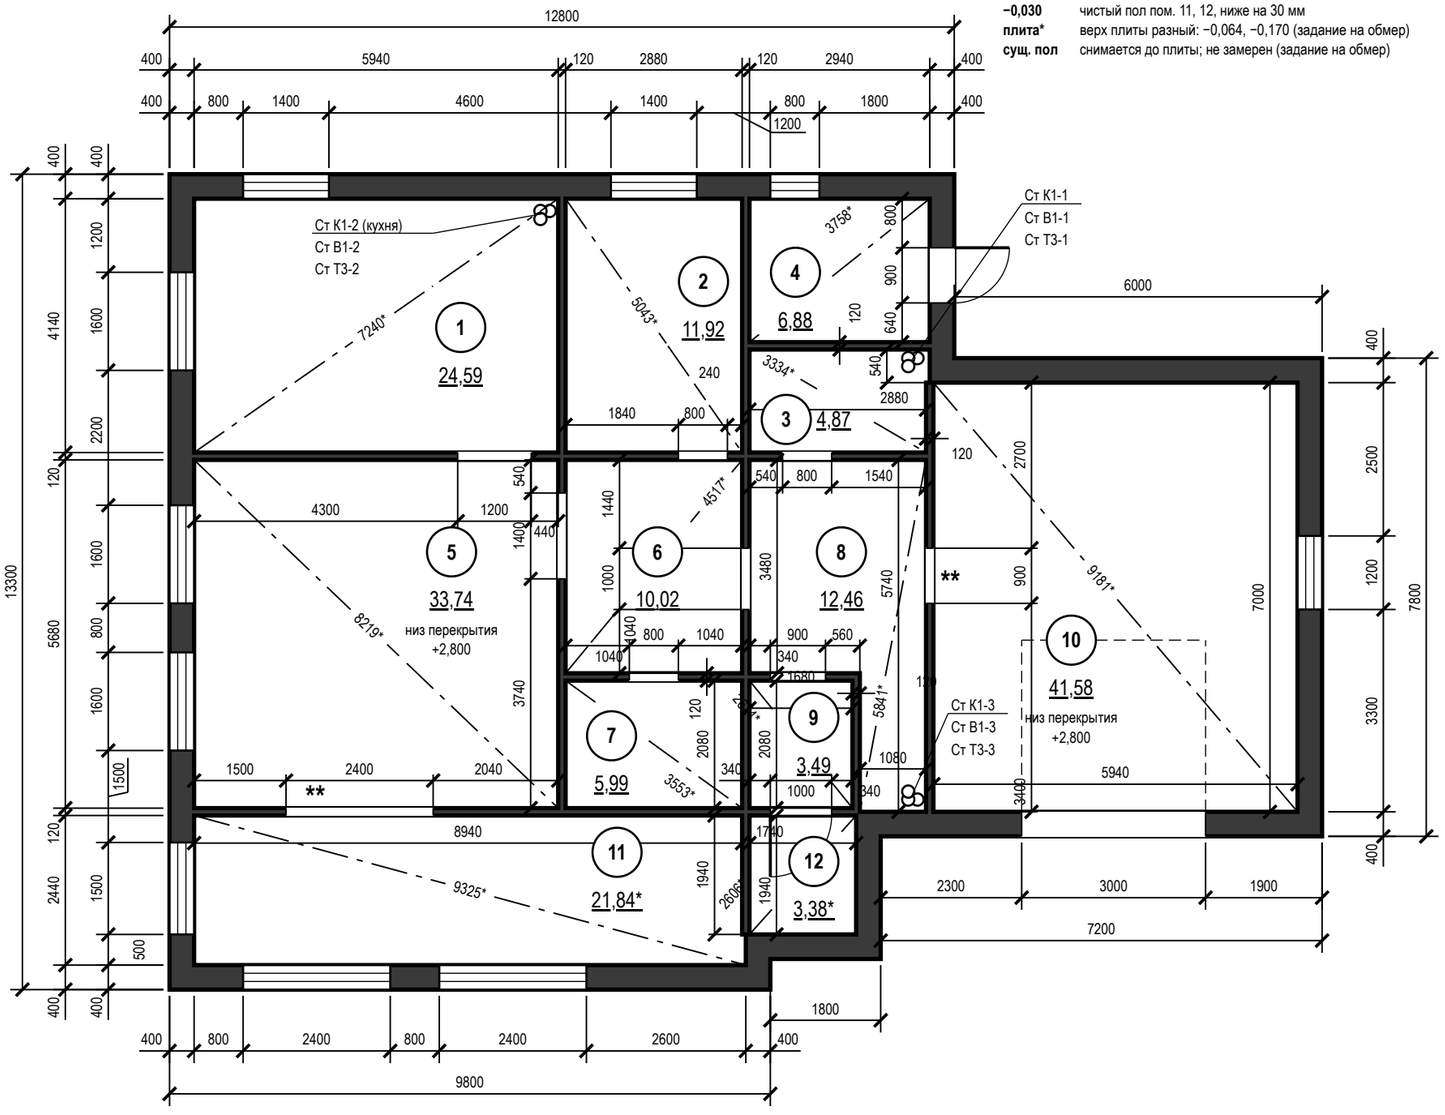

Отметки по высоте

±0,000	чистый пол пом. 1, 2, 4–10; отсчёт высот
−0,015	чистый пол пом. 3, ниже на 15 мм
−0,030	чистый пол пом. 11, 12, ниже на 30 мм
плита*	верх плиты разный: −0,064, −0,170 (задание на обмер)
сущ. пол	снимается до плиты; не замерен (задание на обмер)

Экспликация помещений

№	Наименование	Площадь, м²
1	Кухня-столовая	24,59
2	Кабинет-гостевая	11,92
3	Санузел 1 этажа	4,87
4	Котельная	6,88
5	Гостиная	33,74
6	Холл с лестницей	10,02
7	Кладовая	5,99
8	Прихожая	12,46
9	Тамбур	3,49
10	Гараж	41,58
11	Веранда *	21,84
12	Крыльцо *	3,38
	Итого по этажу	**155,54**
	Итого по дому	**270,67**

Условные обозначения

- существующие стены (сечение)
- окно (рама, остекление)
- проём существующий, без заполнения (откосы)
- стояк: К1 — канализация, В1 — ХВС, Т3 — ГВС
- ** — «**» — предложение проектировщика, заказчиком не утверждено
- диагональ помещения — контроль прямоугольности
- 1 — номер помещения, площадь м²

Принято, не определено или спорно

полностью — листы 8–10

К-1 — Размеры дома на картинке заказчика (470 px) не читаются: состав помещений и форма сняты с картинки, размеры подобраны проектировщиком под площади этажей 185,80 и 145,73 м²

К-2 — Высоты этажей и кровля не известны: приняты 2800 мм (1-й этаж) и 2700 мм (горизонтальная часть потолка мансарды); скаты — двускатная кровля, конёк вдоль длинной стороны, колено 1200 мм, уклон 45° (по перспективе и фасаду с картинки)

К-5 — Планировка этажей — предложение проектировщика по составу помещений с картинки (несущие стены, лестница, перекрытие не известны). нужен проект АР/КР дома

К-13 — Веранда (пом. 11) и крыльцо (пом. 12): чистый пол −0,030, пирог 140 мм (утеплитель XPS 100, сборное основание ГВЛВ 25, клей 5, керамогранит 10) — верх плиты принят −0,170, то есть пол принят на 0,14 ниже (пункт дома (-0,064)-(-0,030)).

Примечания

1. Размеры — в мм по чистым поверхностям стен до отделки (по плану заказчика); площади — в м² по тем же размерам. До начала работ выполнить контрольный обмер.
2. За отметку ±0,000 принят чистый пол 1-го этажа, не существующий (блок отметок). «Низ перекрытия» у марки помещения — отметка низа перекрытия от ±0,000, как на развёртках и плане потолков (не высота потолка: потолок — по плану потолков).
3. Толщины стен: наружные 400 мм, перегородки 120 мм; отличающиеся толщины и уступы размерами на плане.
4. Несущие стены не определены: до технического заключения все стены считать несущими; проёмы и штробы в них не выполнять.
5. Дверные проёмы показаны без заполнения (двери — лист 25); высота дверных проёмов 2100, 2300 мм, проёмов без двери 2100 мм; низ окон (подоконник) 900, 1200 мм от чистого пола, высота окон 1500, 900, 1600 мм.
6. Диагонали — контрольные размеры; «*» — расчёт по принятому контуру (К-1), при обмере заменить замеренным; расхождение более 5 мм подписать на плане как перекос.
7. Размеры проверить на месте до начала работ; расхождение контрольных промеров ≤ 2 %.
8. Помещения, отмеченные *, в общую площадь дома и в итоги не входят.

1000 мм · печать 1:1

Допущения и предложения на листе. Основа листа: размеры и контуры этажей подобраны проектировщиком по составу помещений и площадям этажей с картинки 470 px (размеры на ней не читаются); обмер и исходный проект — задание (К-1); высоты: 1-й этаж 2800 мм, мансарда 2700 мм (горизонтальная часть) приняты; скаты кровли мансарды приняты по картинке: колено 1200 мм, уклон 45°, конёк вдоль длинной стороны; проект КР — задание (К-2); наружные стены 400 мм, перегородки 120 мм приняты (К-1); разрешённая мощность 15 кВт принята по типовым ТУ для частного дома (К-4); подрайон климата не задан — принят не северный (жилые от 2,5 м) (К-7). Знак «**» — предложение проектировщика, заказчиком не утверждено (согласовать с заказчиком). См. лист открытых вопросов (лист 8, записи К-1, К-2, К-4, К-5, К-7; лист 9, записи К-9, К-13); по листу — К-1, К-2, К-5, К-13.


Изм.	Кол.уч	Лист	№ док.	Подп.	Дата			
Разраб.		Кырлан А.С.			04.11.26	ГД-2026-010-АИ		
Пров.						Дом 331 м²		
ГИП						Общая площадь 270,67* м² · * — не замерено (реестр л. 8, 10)		
						Дизайн-проект интерьера	Стадия: РП	Лист: 19 / Листов: 216
Н. контр.						Обмерный план · 1-й этаж	Кырлан Александр Сергеевич	
Утв.						М 1:100		

выпуск 04.11.2026 № 2a77323a49 · стр. 19 из 221

Обмерный план · Мансарда

Существующее положение · размеры в мм · отметки от чистого пола

ПРЕДВАРИТЕЛЬНО · не для производства работ · открыто пунктов: 15 (реестр — л. 8–10)

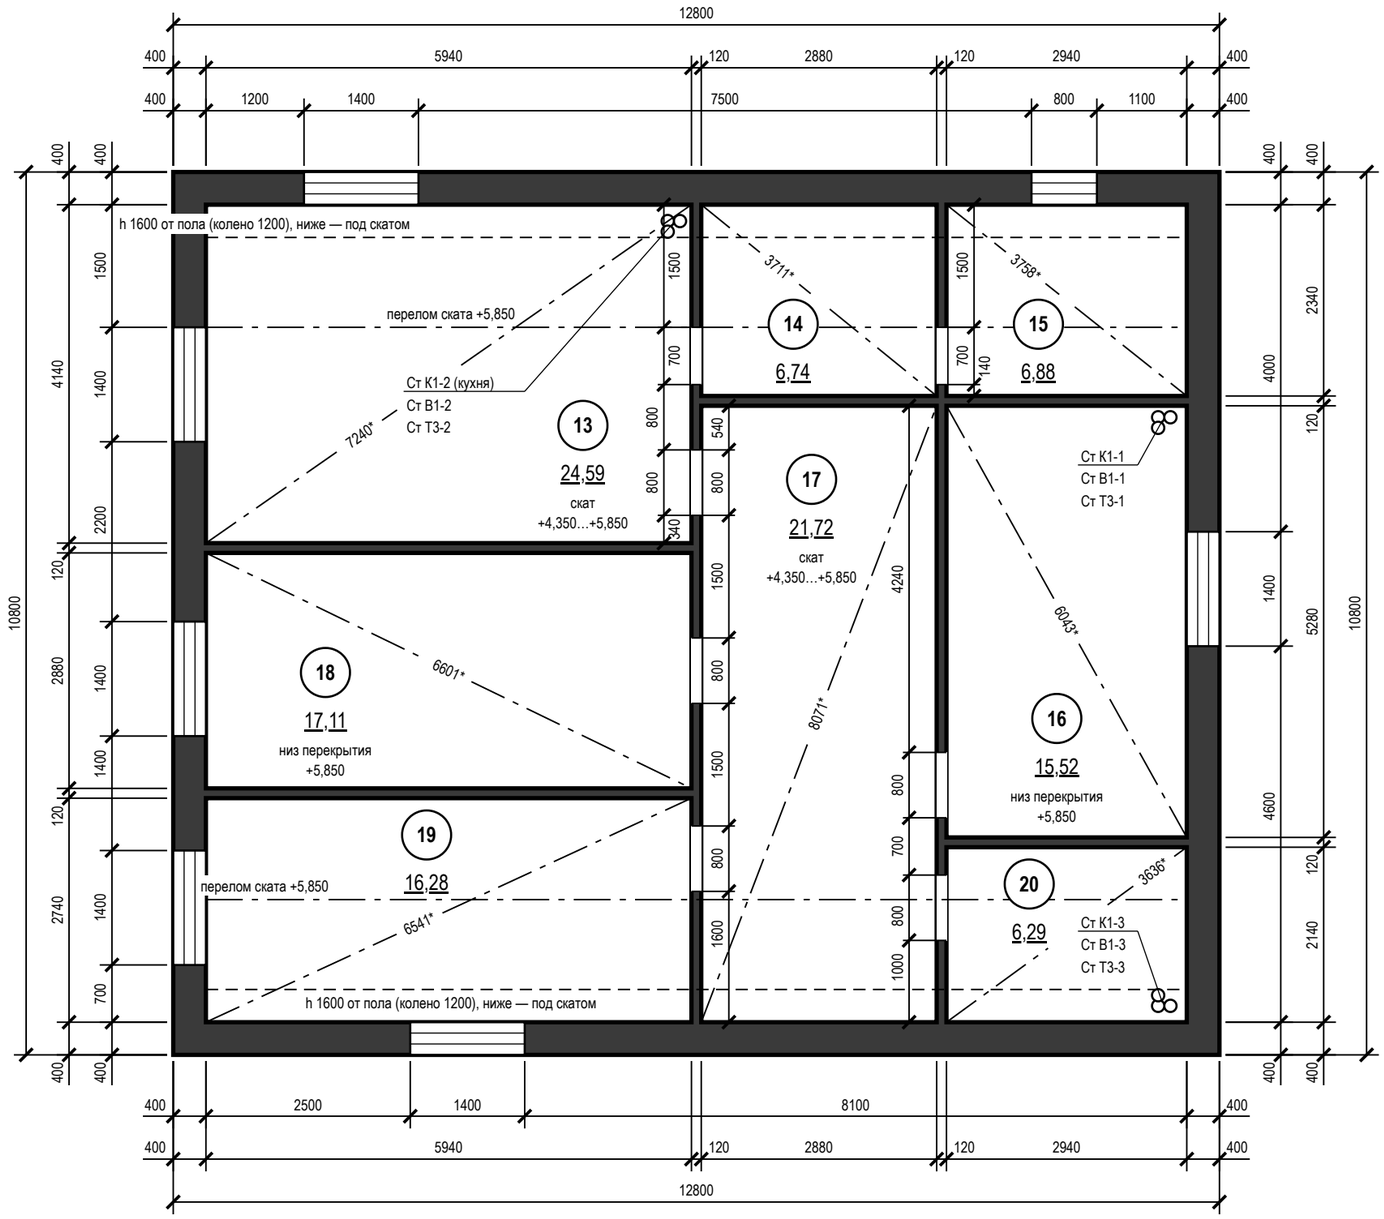

Экспликация помещений

№	Наименование	Площадь, м²
13	Спальня мастер	24,59
14	Гардеробная мастер	6,74
15	Санузел мастер	6,88
16	Спальня 2	15,52
17	Холл мансарды	21,72
18	Спальня 3	17,11
19	Спальня 4	16,28
20	Санузел 2	6,29
	Итого по этажу	**115,13**

Условные обозначения

- существующие стены (сечение)
- окно (рама, остекление)
- проём существующий, без заполнения (откосы)
- стояк: К1 — канализация, В1 — ХВС, Т3 — ГВС
- диагональ помещения — контроль прямоугольности
- (1) номер помещения, площадь м²

Примечания

1. Размеры — в мм по чистым поверхностям стен до отделки (по плану заказчика); площади — в м² по тем же размерам. До начала работ выполнить контрольный обмер.
2. За отметку ±0,000 принят чистый пол 1-го этажа, не существующий; чистый пол этажа +3,150 (блок отметок). «Низ перекрытия» у марки помещения — отметка низа перекрытия от ±0,000, как на развёртках и плане потолков (не высота потолка: потолок — по плану потолков).
3. Толщины стен: наружные 400 мм, перегородки 120 мм, отличающиеся толщины и уступы размерами на плане.
4. Несущие стены не определены: до технического заключения все стены считать несущими; проёмы и штробы в них не выполнять.
5. Дверные проёмы показаны без заполнения (двери — лист 25); высота дверных проёмов 2100 мм; низ окон (подоконник) 900, 1500 мм от чистого пола; высота окон 1500, 800 мм.
6. Диагонали — контрольные размеры; «*» — расчёт по принятому контуру (К-1), при обмере заменить замеренным; расхождение более 5 мм подписать на плане как перекос.
7. Размеры проверить на месте до начала работ; расхождение контрольных проверок ≤ 2 %.

Принято, не определено или спорно

полностью — плиты 8–10.

К-1 — Размеры дома на картинке заказчика (470 px) не читаются; состав помещений и форма сняты с картинки, размеры подобраны проектировщиком под площади этажей 185,80 и 145,73 м².

К-2 — Высоты этажей и кровля не известны; приняты 2800 мм (1-й этаж) и 2700 мм (горизонтальная часть потолка мансарды); скаты — двускатная кровля, конёк вдоль длинной стороны, колено 1200 мм, уклон 45° (по перспективе и фасаду с картинки).

К-5 — Планировка этажей — предложение проектировщика по составу помещений с картинки (несущие стены, лестница, перекрытие не известны): нужен проект АР/КР дома.

К-13 — Веранда (пом. 11) и крыльцо (пом. 12): чистый пол −0,030, пирог 140 мм (утеплитель XPS 100, сборное основание ГВЛВ 25, клей 5, керамогранит 10) — верх плиты принят −0,170, то есть своя плита на 106 мм ниже плиты дома (−0,064).

Отметки по высоте

±0,000	чистый пол 1-го этажа; отсчёт отметок
+3,150*	чистый пол пом. 13, 14, 16–19 (мансарда)
+3,135*	чистый пол пом. 15, 20, ниже на 15 мм
+3,086*	верх плиты — расчёт, не замер (задание на обмер)
сущ. пол	снимается до плиты; не замерен (задание на обмер)

Допущения и предложения на листе

Основа листа: размеры и контуры этажей подобраны проектировщиком по составу помещений и площадям этажей с картинки 470 px (размеры на ней не читаются); обмер и исходный проект — задание (К-1); высоты: 1-й этаж 2800 мм, мансарда 2700 мм (горизонтальная часть) приняты; скаты кровли мансарды приняты по картинке: колено 1200 мм, уклон 45°, конёк вдоль длинной стороны; проект КР — задание (К-2); наружные стены 400 мм, перегородки 120 мм приняты (К-1); разрешённая мощность 15 кВт принята по типовым ТУ для частного дома (К-4); подрайон климата не задан — принят не северный (жилые от 2,5 м) (К-7).

Знак «*» — принято, не замерено и не подтверждено (замерить на объекте): К-2: отметка чистого пола этажа «Мансарда» +3,150 — принята без источника, все отметки мансарды считаются от неё.

Открытые вопросы и конфликты по листу: К-1, К-2, К-5, К-13.

См. лист открытых вопросов (лист 8, записи К-1, К-2, К-4, К-5, К-7; лист 9, запись К-13).

1000 мм · печать 1:1

Изм.	Кол.уч	Лист	№ док.	Подп.	Дата
Разраб.		Кырлан А.С.			04.11.26
Пров.					
ГИП					
Н. контр.					
Утв.					

ГД-2026-010-АИ

Дом 331 м²

Общая площадь 270,67* м² · * размеры приняты, не замерены (реестр — л. 8–10, К-1)

Дизайн-проект интерьера

Стадия	Лист	Листов
РП	20	216

Обмерный план · Мансарда


М 1:75

Кырлан Александр Сергеевич

выпуск 04.11.2026 № 2a77323a49 · стр. 20 из 221

План демонтажа и монтажа перегородок · 1-й этаж

Перепланировка не выполняется · существующие стены сохраняются · размеры в мм

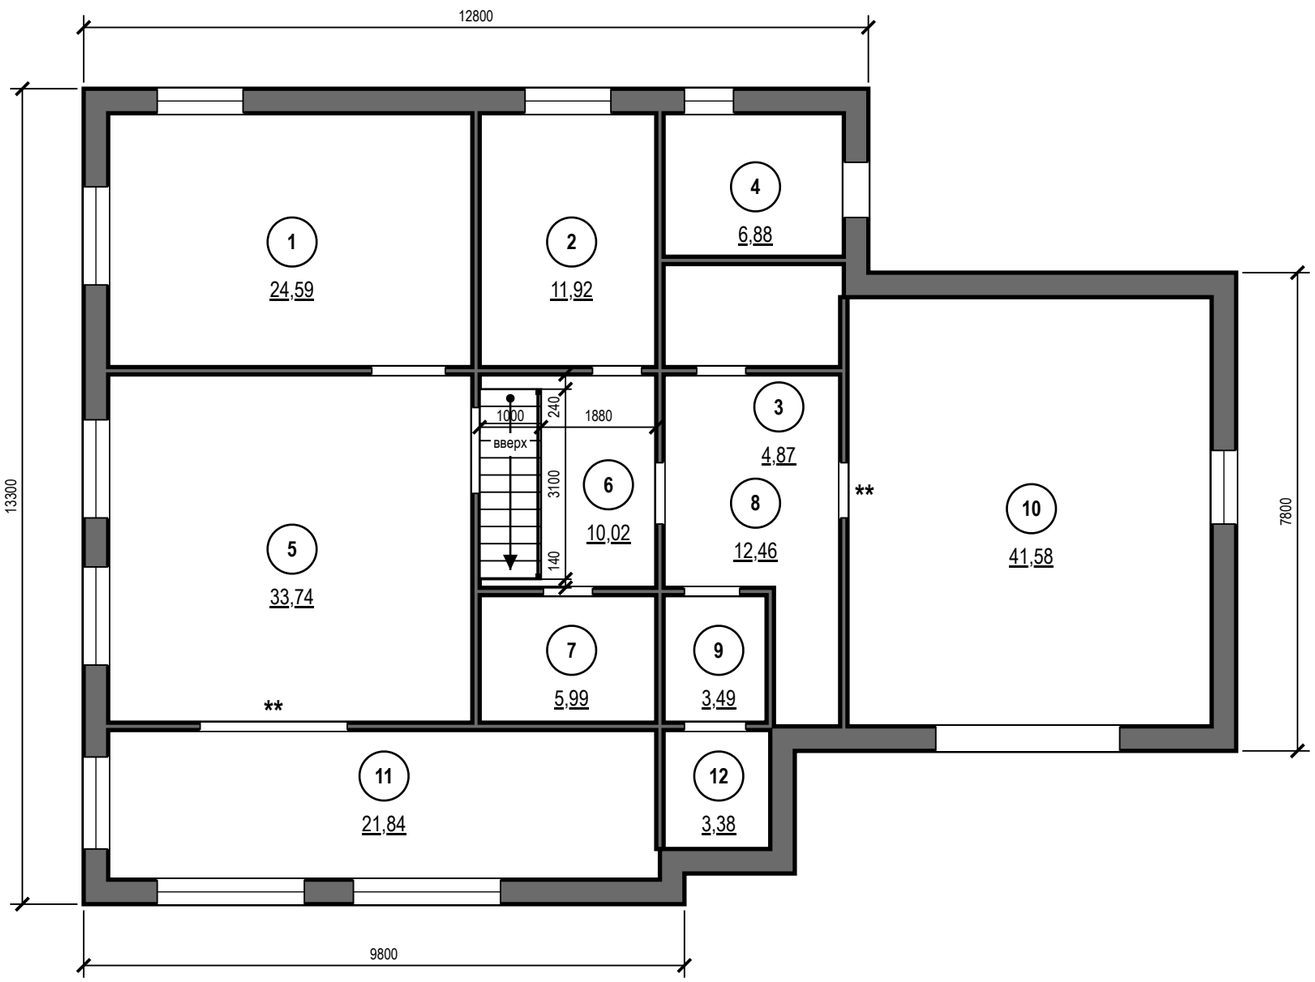

Условные обозначения

- существующие стены — сохраняются;
- несущие не определены — считать несущими
- демонтируемые конструкции — на плане нет
- возводимые перегородки — на плане нет
- проём существующий, без заполнения (откосы)
- (1) номер помещения, площадь м²

Отметки по высоте

±0,000	чистый пол пом. 1, 2, 4–10; отсчёт высот	**плита***	верх плиты разный: −0,064, −0,170 (задание на обмер)
−0,015	чистый пол пом. 3, ниже на 15 мм	**сущ. пол**	снимается до плиты; не замерен (задание на обмер)
−0,030	чистый пол пом. 11, 12, ниже на 30 мм		

Примечания

1. Перепланировка не выполняется: несущие и ненесущие стены, перегородки и плиты перекрытия не демонтируются, новые стены не возводятся; существующие стены и перегородки сохраняются.
2. Дверные блоки — по плану дверей; существующие проёмы не расширяются.
3. Демонтаж существующих покрытий пола, стен и потолка, дверных блоков и сантехприборов (если есть) — до основания; объёмы демонтажа — для справки, по факту на объекте.
4. За отметку ±0,000 принят чистый пол 1-го этажа, не существующий (блок отметок). Размеры — в мм по чистовой поверхности стен до отделки.
5. Размеры проверить на месте до начала работ: расхождение с обмером — не более 2 % (иначе — к архитектору).
6. Несущие стены не определены: до технического заключения все стены считать несущими — проёмы, ниши и штробы в них не выполнять.

Допущения и предложения на листе

Основа листа: размеры и контуры этажей подобраны проектировщиком по составу помещений и площадям этажей с картинки 470 px (размеры на ней не читаются); обмер и исходный проект — задание (К-1); высоты: 1-й этаж 2800 мм, мансарда 2700 мм (горизонтальная часть) приняты; скаты кровли мансарды приняты по картинке: колено 1200 мм, уклон 45°, конёк вдоль длинной стороны; проект КР — задание (К-2); наружные стены 400 мм, перегородки 120 мм приняты (К-1); разрешённая мощность 15 кВт принята по типовым ТУ для частного дома (К-4); подрайон климата не задан — принят не северный (жилые от 2,5 м) (К-7).

Знак «**» — предложение проектировщика, заказчиком не утверждено (согласовать с заказчиком): дверь пом. 8 (стена Б) — дверь гаража в дом — СП 55.13330.2016 п. 7.7: EI 30, уплотнение в притворах, самозакрывание (доводчик); К-9: дверь пом. 5 (стена В) — проём 2400×2100 на веранду с картинки: одной распашной створкой не закрывается (полотна 600–900) — раздвижная двустворчатая, остеклённая; система и полотна — по каталогу после утверждения автором.

См. лист открытых вопросов (лист 8, записи К-1, К-2, К-4, К-7; лист 9, запись К-9).

1000 мм · печать 1:1

Изм.	Кол.уч	Лист	№ док.	Подп.	Дата
Разраб.		Кырлан А.С.			04.11.26
Пров.					
ГИП					
Н. контр.					
Утв.					

ГД-2026-010-АИ

Дом 331 м²

Общая площадь 270,67* м² · * размеры приняты, не замерены (реестр — л. 8–10, К-1)

Дизайн-проект интерьера

Стадия	Лист	Листов
РП	21	216

План демонтажа и монтажа перегородок · 1-й этаж

М 1:100


Кырлан Александр Сергеевич

выпуск 04.11.2026 № 2a77323a49 · стр. 21 из 221

План демонтажа и монтажа перегородок · Мансарда

Перепланировка не выполняется · существующие стены сохраняются · размеры в мм

ПРЕДВАРИТЕЛЬНО · не для производства работ · открыто пунктов: 15 (реестр — л. 8–10)

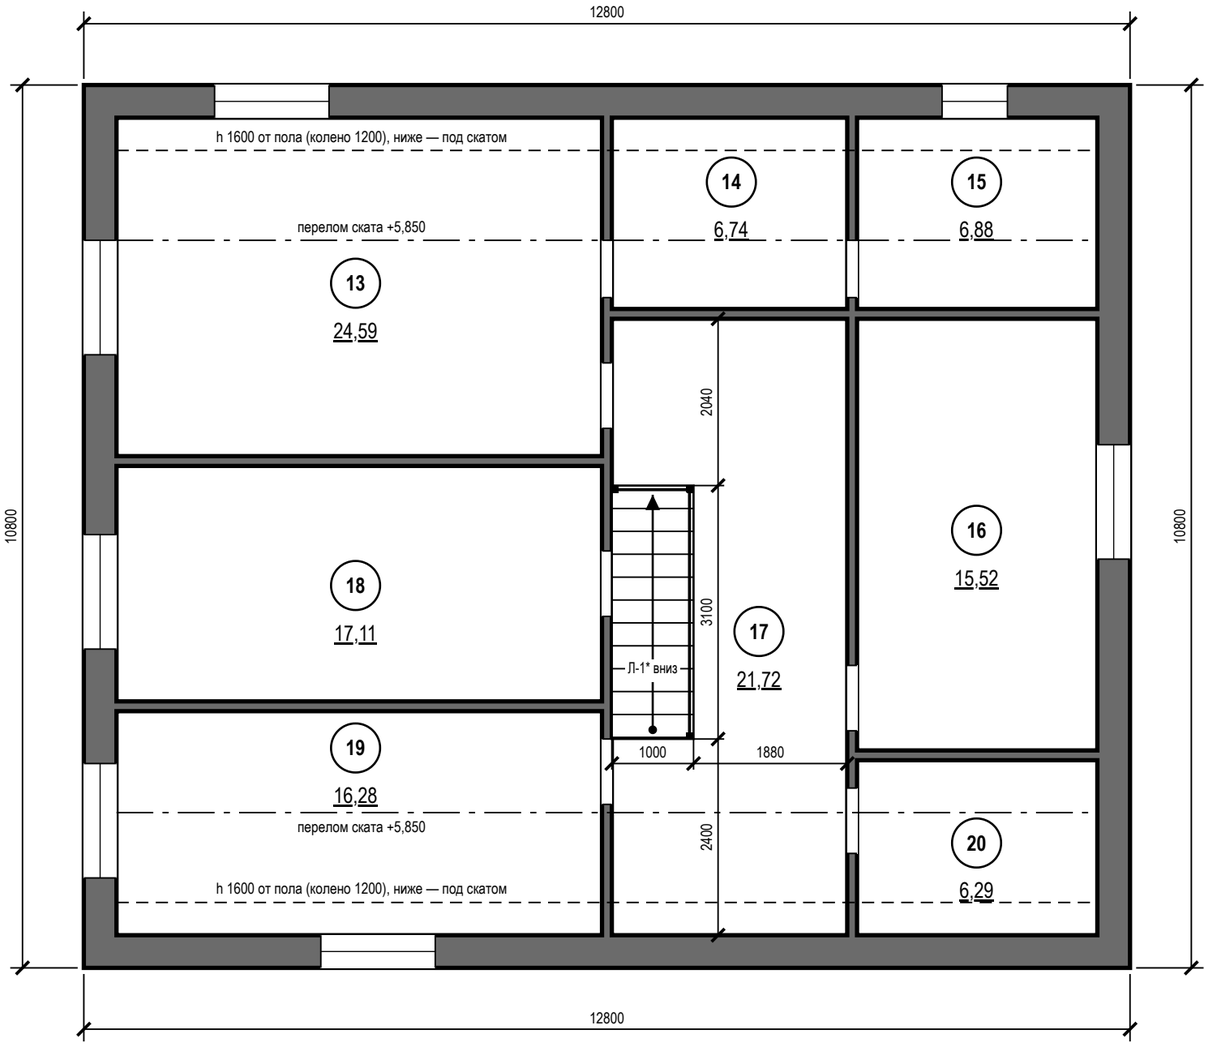

Условные обозначения

- существующие стены — сохраняются;
- несущие не определены — считать несущими
- демонтируемые конструкции — на плане нет
- возводимые перегородки — на плане нет
- проём существующий, без заполнения (откосы)
- (1) номер помещения, площадь м²

Отметки по высоте

±0,000	чистый пол 1-го этажа; отсчёт отметок	**+3,086***	верх плиты — расчёт, не замер (задание на обмер)
+3,150*	чистый пол пом. 13, 14, 16–19 (мансарда)	**сущ. пол**	снимается до плиты; не замерен (задание на обмер)
+3,135*	чистый пол пом. 15, 20, ниже на 15 мм		

Допущения и предложения на листе

Основа листа: размеры и контуры этажей подобраны проектировщиком по составу помещений и площадям этажей с картинки 470 px (размеры на ней не читаются); обмер и исходный проект — задание (К-1); высоты: 1-й этаж 2800 мм, мансарда 2700 мм (горизонтальная часть) приняты; скаты кровли мансарды приняты по картинке: колено 1200 мм, уклон 45°, конёк вдоль длинной стороны; проект КР — задание (К-2); наружные стены 400 мм, перегородки 120 мм приняты (К-1); разрешённая мощность 15 кВт принята по типовым ТУ для частного дома (К-4); подрайон климата не задан — принят не северный (жилые от 2,5 м) (К-7).

Знак «*» — принято, не замерено и не подтверждено (замерить на объекте): К-2: отметка чистого пола этажа «Мансарда» +3,150 — принята без источника, все отметки мансарды считаются от неё; К-6: Л-1 — габарит марша снят с картинки заказчика (11 проступей в холле 3,6 м), а до отм. +3,150 нужно 18 подъёмов — одномаршевая не встаёт: решение по К-6.

См. лист открытых вопросов (лист 8, записи К-1, К-2, К-4, К-6, К-7).

Примечания

1. Перепланировка не выполняется: несущие и ненесущие стены, перегородки и плиты перекрытия не демонтируются, новые стены не возводятся; существующие стены и перегородки сохраняются.
2. Дверные блоки — по плану дверей; существующие проёмы не расширяются.
3. Демонтаж существующих покрытий пола, стен и потолка, дверных блоков и сантехприборов (если есть) — до основания; объёмы демонтажа — для справки, по факту на объекте.
4. За отметку ±0,000 принят чистый пол 1-го этажа, не существующий; чистый пол этажа +3,150 (блок отметок). Размеры — в мм по чистовой поверхности стен до отделки.
5. Размеры проверить на месте до начала работ: расхождение с обмером — не более 2 % (иначе — к архитектору).
6. Несущие стены не определены: до технического заключения все стены считать несущими — проёмы, ниши и штробы в них не выполнять.

1000 мм · печать 1:1

Изм.	Кол.уч	Лист	№ док.	Подп.	Дата
Разраб.		Кырлан А.С.			04.11.26
Пров.					
ГИП					
Н. контр.					
Утв.					

ГД-2026-010-АИ

Дом 331 м²

Общая площадь 270,67* м² · * размеры приняты, не замерены (реестр — л. 8–10, К-1)

Дизайн-проект интерьера

Стадия	Лист	Листов
РП	22	216

План демонтажа и монтажа перегородок · Мансарда

М 1:75

Кырлан Александр Сергеевич


выпуск 04.11.2026 № 2a77323a49 · стр. 22 из 221

План дверей · 1-й этаж

Проёмы, марки заполнения, привязки · размеры в мм

Условные обозначения

- стены (подложка обмера)
- дверь распашная, дуга открывания
- дверь скрытого монтажа
- дверь входная (полотно толще)
- ворота подъёмно-секционные (ход полотна)
- дверь раздвижная
- портал (штрих — перемычка)
- оконный блок
- Д — марка типа (Д-N, ПР-N, ОК-N)
- 1 — номер помещения, площадь м²
- ** — «**» — предложение проектировщика, заказчиком не утверждено

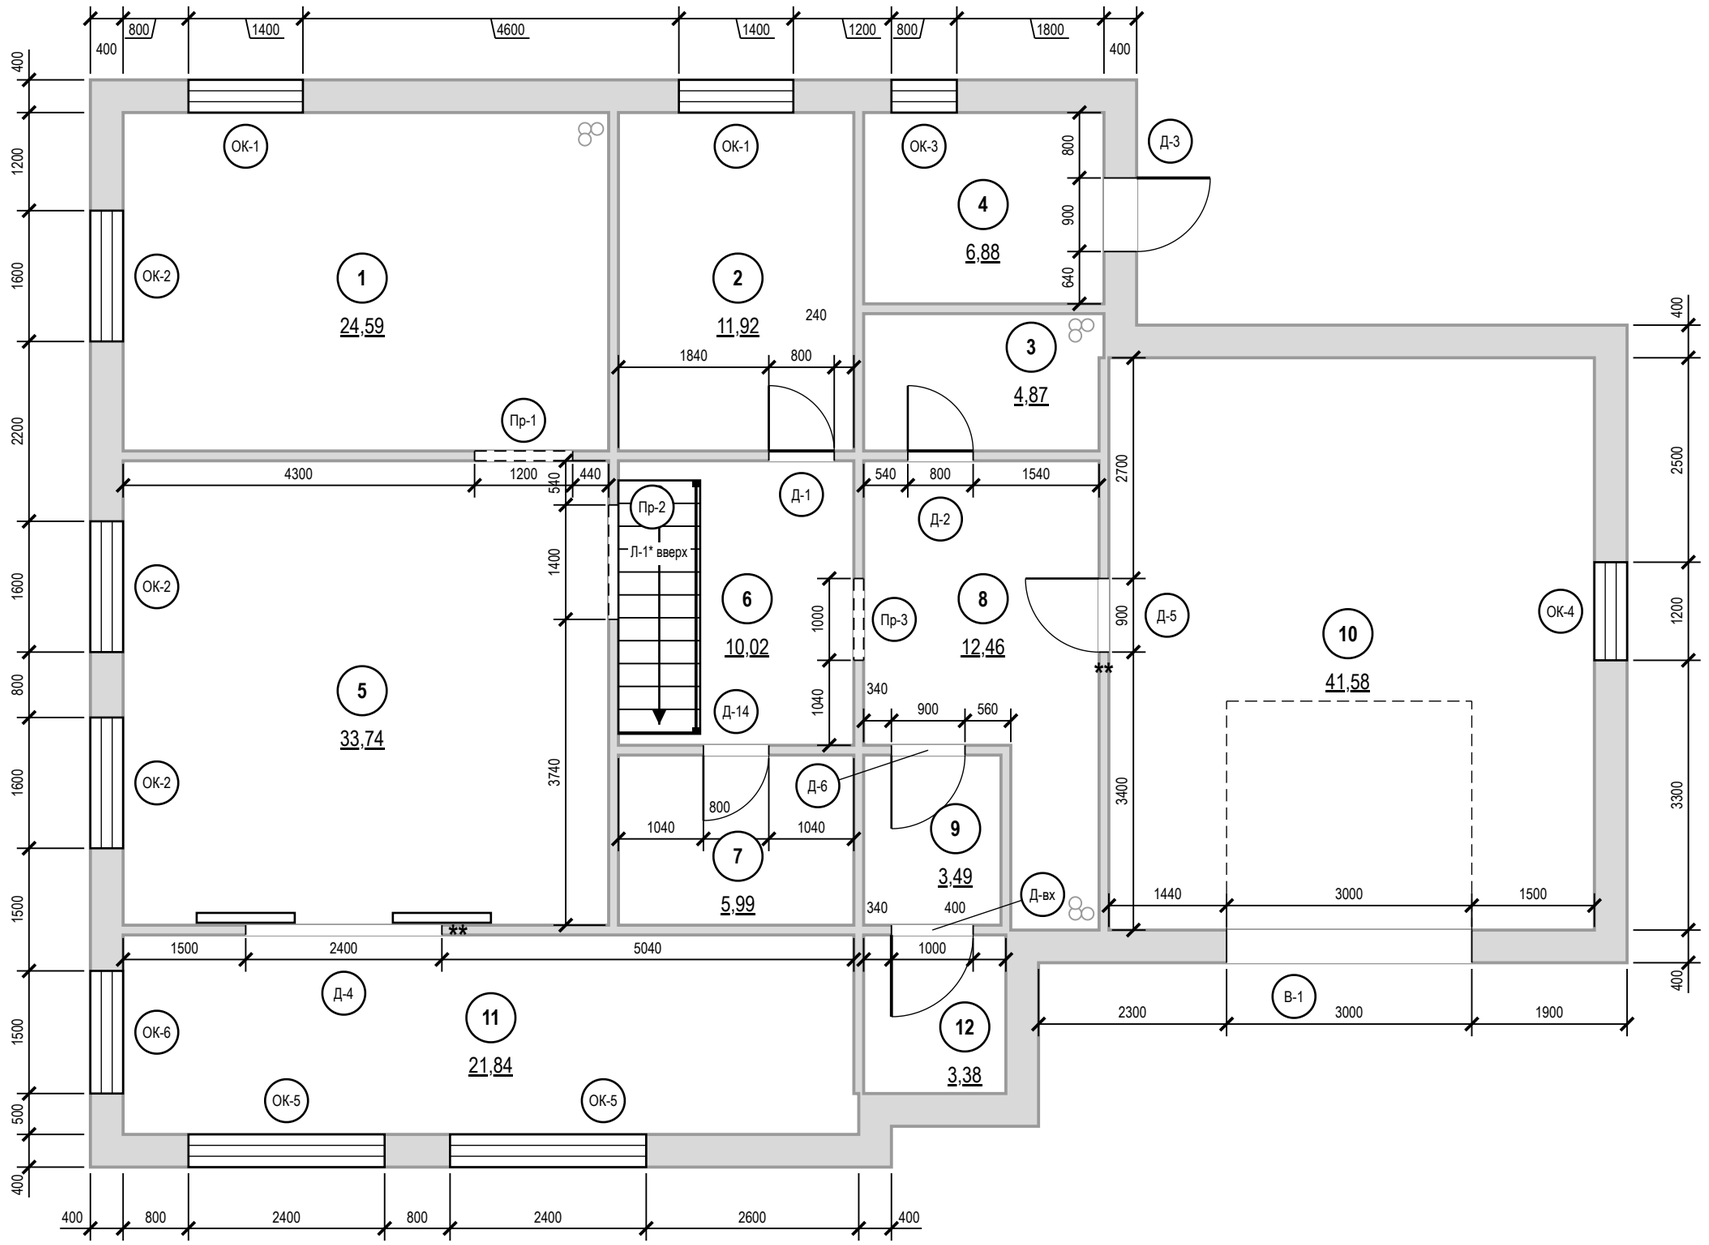

Допущения и предложения на листе

Основа листа: размеры и контуры этажей подобраны проектировщиком по составу помещений и площадям этажей с картинки 470 px (размеры на ней не читаются); обмер и исходный проект — задание (К-1); высоты: 1-й этаж 2800 мм, мансарда 2700 мм (горизонтальная часть) приняты; скаты кровли мансарды приняты по картинке: колено 1200 мм, уклон 45°, конёк вдоль длинной стороны; проект КР — задание (К-2); наружные стены 400 мм, перегородки 120 мм приняты (К-1); разрешённая мощность 15 кВт принята по типовым ТУ для частного дома (К-4); подрайон климата не задан — принят не северный (жилые от 2,5 м) (К-7).

Знак «*» — принято, не замерено и не подтверждено (замерить на объекте): К-6: Л-1 — габарит марша снят с картинки заказчика (11 проступей в холле 3,6 м), а до отм. +3,150 нужно 18 подъёмов — одномаршевая не встаёт: решение по К-6.

Знак «**» — предложение проектировщика, заказчиком не утверждено (согласовать с заказчиком): дверь пом. 8 (стена Б) — дверь гаража в дом — СП 55.13330.2016 п. 7.7: EI 30, уплотнение в притворах, самозакрывание (доводчик); К-9: дверь пом. 5 (стена В) — проём 2400×2100 на веранду с картинки: одной распашной створкой не закрывается (полотна 600–900) — раздвижная двустворчатая, остеклённая; система и полотна — по каталогу после утверждения автором.

Открытые вопросы и конфликты по листу: К-9.

См. лист открытых вопросов (лист 8, записи К-1, К-2, К-4, К-6, К-7; лист 9, запись К-9).

Примечания

1. Размеры проёмов и привязки — в миллиметрах от чистых граней стен до отделки; привязка — от угла того помещения, со стороны которого стоит размер. Размер проёма — ширина × высота от чистого пола 0,000. Размеры на плане — проёмов, не полотен: полотно — в ведомости, коробка — по системе.
2. Марки в кружках — типы заполнения проёмов (ГОСТ 21.501-2018, п. 5.3.2); одна марка — один типоразмер; количество сверено с планом.
3. Д-1, Д-2 — существующие проёмы, до техзаключения не расширять.
4. Д-3, Д-вх, В-1: дуга наружу — по плану заказчика, не проверено; блок оставить или заменить — не решено.
5. Ведомость заполнения проёмов, открывание полотен, заказ и порядок монтажа блоков — лист 25.

1000 мм · печать 1:1

Изм.	Кол.уч	Лист	№ док.	Подп.	Дата
Разраб.		Кырлан А.С.			04.11.26
Пров.					
ГИП					
Н. контр.					
Утв.					

ГД-2026-010-АИ

Дом 331 м²

Общая площадь 270,67* м² · * размеры приняты, не замерены (реестр — л. 8–10, К-1)

Дизайн-проект интерьера

Стадия	Лист	Листов
РП	23	216

План дверей · 1-й этаж


М 1:75

Кырлан Александр Сергеевич

выпуск 04.11.2026 № 2a77323a49 · стр. 23 из 221

План дверей · Мансарда

Проёмы, марки заполнения, привязки · размеры в мм

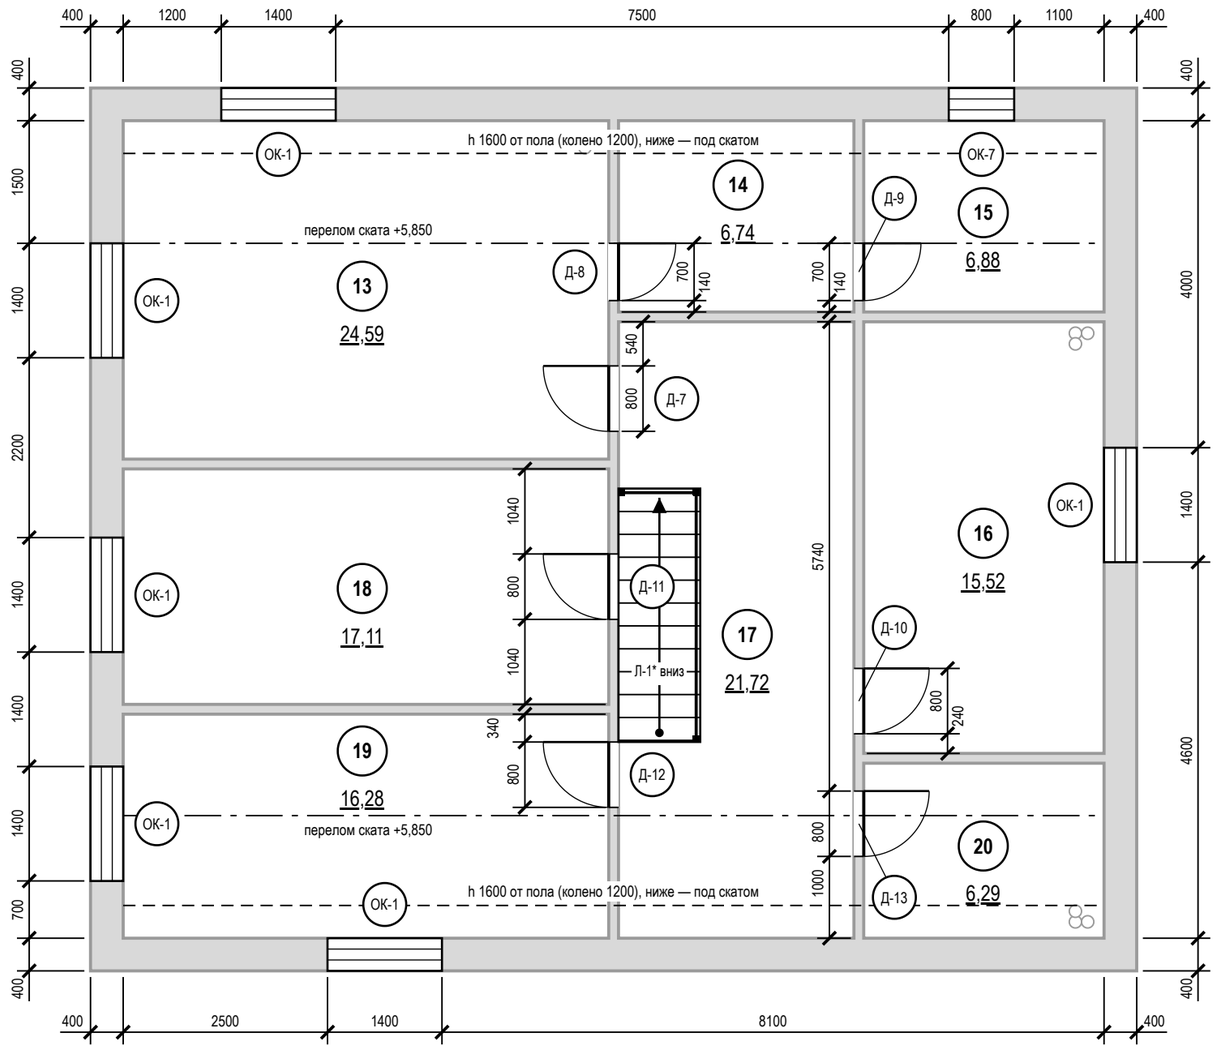

Условные обозначения

- стены (подложка обмера)
- дверь распашная, дуга открывания
- дверь скрытого монтажа
- оконный блок
- Д — марка типа (Д-N, ПР-N, ОК-N)
- 1 — номер помещения, площадь м²

Примечания

1. Размеры проёмов и привязки — в миллиметрах от чистых граней стен до отделки; привязка — от угла того помещения, со стороны которого стоит размер. Размер проёма — ширина × высота от чистого пола 0,000. Размеры на плане — проёмов, не полотен: полотно — в ведомости, коробка — по системе. Откос от угла помещения до проёма с коробкой — не менее 50 мм.
2. Марки в кружках — типы заполнения проёмов (ГОСТ 21.501-2018, п. 5.3.2); одна марка — один типоразмер; количество сверено с планом.
3. Д-7…Д-13 — существующие проёмы, до техзаключения не расширять.
4. Ведомость заполнения проёмов, открывание полотен, заказ и порядок монтажа блоков — лист 25.

Допущения и предложения на листе

Основа листа: размеры и контуры этажей подобраны проектировщиком по составу помещений и площадям этажей с картинки 470 px (размеры на ней не читаются); обмер и исходный проект — задание (К-1); высоты: 1-й этаж 2800 мм, мансарда 2700 мм (горизонтальная часть) приняты; скаты кровли мансарды приняты по картинке: колено 1200 мм, уклон 45°, конёк вдоль длинной стороны; проект КР — задание (К-2); наружные стены 400 мм, перегородки 120 мм приняты (К-1); разрешённая мощность 15 кВт принята по типовым ТУ для частного дома (К-4); подрайон климата не задан — принят не северный (жилые от 2,5 м) (К-7).

Знак «*» — принято, не замерено и не подтверждено (замерить на объекте): К-2: отметка чистого пола этажа «Мансарда» +3,150 — принята без источника, все отметки мансарды считаются от неё; К-6: Л-1 — габарит марша снят с картинки заказчика (11 проступей в холле 3,6 м), а до отм. +3,150 нужно 18 подъёмов — одномаршевая не встаёт: решение по К-6. Открытые вопросы и конфликты по листу: К-9.

См. лист открытых вопросов (лист 8, записи К-1, К-2, К-4, К-6, К-7; лист 9, запись К-9).

1000 мм · печать 1:1

Изм.	Кол.уч	Лист	№ док.	Подп.	Дата
Разраб.		Кырлан А.С.			04.11.26
Пров.					
ГИП					
Н. контр.					
Утв.					

ГД-2026-010-АИ

Дом 331 м²

Общая площадь 270,67* м² · * размеры приняты, не замерены (реестр — л. 8–10, К-1)

Дизайн-проект интерьера

Стадия	Лист	Листов
РП	24	216

План дверей · Мансарда

М 1:75

Кырлан Александр Сергеевич

Ведомость заполнения проёмов

Проёмы, полотна, отделка, фурнитура · размеры в мм


Ведомость заполнения проёмов

Марка	Наименование, обозначение	Проём ш×в, мм	Полотно (расч.)	Кол.	Откр.	Отделка полотна	Фурнитура	Прим.
Д-вх	Блок дверной входной, ГОСТ 31173-2016	1000×2100	блок задать	1	Л	в комплекте блока	в комплекте блока (замки, глазок)	наружу
В-1	Ворота подъёмно-секционные, по каталогу изготовителя	3000×2300	не задано (записи реестра нет)	1		в комплекте ворот	в комплекте ворот (направляющие, привод)	
Д-1	Дверь скрытого монтажа, UNION FILO-60 Piatto	800×2100	700×2000	1	П	окраска No. 226 с двух сторон	скрытые петли 3D, магнитный замок	
Д-2	Дверь скрытого монтажа, UNION FILO-60 Piatto	800×2100	700×2000	1	П	в тон облицовки — пом. 3, No. 226 — пом. 8	скрытые петли 3D, магнитный замок, фиксатор WC	порог 15
Д-3	Блок дверной входной, ГОСТ 31173-2016	900×2100	блок задать	1	П	в комплекте блока	в комплекте блока (замки, глазок)	наружу
Д-4	Дверь раздвижная двустворчатая, остекл., ГОСТ 475-2016	2400×2100	не задано (записи реестра нет)	1			раздвижная система, ручки-купе	** пом. 5
Д-5	Блок дверной внутренний, ГОСТ 475-2016	900×2100	800×2000	1	Л		петли, ручка с защёлкой	** пом. 8; EI 30
Д-6	Блок дверной внутренний, ГОСТ 475-2016	900×2100	800×2000	1	Л		петли, ручка с защёлкой	
Д-7	Дверь скрытого монтажа, UNION FILO-60 Piatto	800×2100	700×2000	1	Л	окраска No. 226 с двух сторон	скрытые петли 3D, магнитный замок	
Д-8	Дверь скрытого монтажа, UNION FILO-60 Piatto	700×2100	600×2000	1	П	No. 105 — пом. 14, No. 226 — пом. 13	скрытые петли 3D, магнитный замок	
Д-9	Дверь скрытого монтажа, UNION FILO-60 Piatto	700×2100	600×2000	1	П	в тон облицовки — пом. 15, No. 105 — пом. 14	скрытые петли 3D, магнитный замок, фиксатор WC	порог 15
Д-10	Дверь скрытого монтажа, UNION FILO-60 Piatto	800×2100	700×2000	1	П	окраска No. 226 с двух сторон	скрытые петли 3D, магнитный замок	
Д-11	Дверь скрытого монтажа, UNION FILO-60 Piatto	800×2100	700×2000	1	Л	окраска No. 226 с двух сторон	скрытые петли 3D, магнитный замок	
Д-12	Дверь скрытого монтажа, UNION FILO-60 Piatto	800×2100	700×2000	1	Л	окраска No. 226 с двух сторон	скрытые петли 3D, магнитный замок	
Д-13	Дверь скрытого монтажа, UNION FILO-60 Piatto	800×2100	700×2000	1	П	в тон облицовки — пом. 20, No. 226 — пом. 17	скрытые петли 3D, магнитный замок, фиксатор WC	порог 15
Д-14	Блок дверной внутренний, ГОСТ 475-2016	800×2100	700×2000	1	Л		петли, ручка с защёлкой	
Пр-1	Портал без заполнения	1200×2100		1				б/п
Пр-2	Портал без заполнения	1400×2100		1				б/п
Пр-3	Портал без заполнения	1000×2100		1				б/п
ОК-1	Блок оконный, ГОСТ 23166-2021	1400×1500		8				низ 900
ОК-2	Блок оконный, ГОСТ 23166-2021	1600×1500		3				низ 900
ОК-3	Блок оконный, ГОСТ 23166-2021	800×900		1				низ 1200
ОК-4	Блок оконный, ГОСТ 23166-2021	1200×900		1				низ 1200
ОК-5	Блок оконный, ГОСТ 23166-2021	2400×1600		2				низ 900
ОК-6	Блок оконный, ГОСТ 23166-2021	1500×1600		1				низ 900
ОК-7	Блок оконный, ГОСТ 23166-2021	800×800		1				низ 1500

Примечания

1. Марки проёмов — те же, что на планах дверей этажей (листы 23, 24); привязки проёмов — там же; количество — по всем этажам дома.
2. Открывание: Л — петли слева, П — справа, если смотреть со стороны, куда открывается полотно (на себя).
3. Дверные блоки обычного монтажа (Д-4…Д-6, Д-14) заказывать после чистовой стяжки и штукатурки, проёмы перемерить; монтажный зазор коробки 10–15 мм на сторону, откос от угла помещения до коробки — не менее 50 мм.
4. Скрытые двери (Д-1, Д-2, Д-7…Д-13): проём замерить в чистоте; блок заказать до штукатурки (≈ 30 дн.), короб ставить до штукатурки; полотно навесить после чистовой отделки, красить в цвет стен. Порядок — практика монтажа, изготовитель подтверждает.
5. Полотно «расч.» — по проёму и ряду изделия с запасом по каталогам, заказ — по таблице проёмов модели; Д-1, Д-2, Д-7…Д-13: проём 2100, а под полотно 2000 по каталогам нужен 2050–2080, под 2100 — 2150–2180: высоту проёма — по модели; Д-5, Д-6, Д-14: проём 2100, а под полотно 2000 по каталогам нужен 2040–2080, под 2100 — 2140–2180: высоту проёма — по модели; Д-вх: входной блок по ГОСТ 31173-2016 — задать при выборе блока; Д-3: входной блок по ГОСТ 31173-2016 — задать при выборе блока; Д-4: раздвижная, полотно — по системе — полотно задать при выборе модели.

Схемы дверных блоков (1:40) — вид со стороны открывания; вершина треугольника — сторона петель — продолжение на листе 26

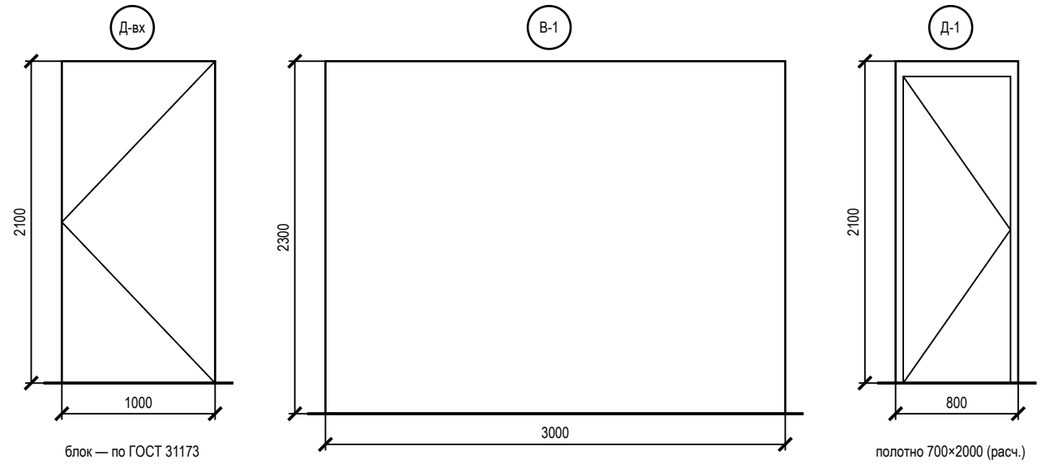

Допущения и предложения на листе

Основа листа: размеры и контуры этажей подобраны проектировщиком по составу помещений и площадям этажей с картинки 470 px (размеры на ней не читаются); обмер и исходный проект — задание (К-1); высоты: 1-й этаж 2800 мм, мансарда 2700 мм (горизонтальная часть) приняты; скаты кровли мансарды приняты по картинке: колено 1200 мм, уклон 45°, конёк вдоль длинной стороны; проект КР — задание (К-2); наружные стены 400 мм, перегородки 120 мм приняты (К-1); разрешённая мощность 15 кВт принята по типовым ТУ для частного дома (К-4); подрайон климата не задан — принят не северный (жилые от 2,5 м) (К-7).

См. лист открытых вопросов (лист 8, записи К-1, К-2, К-4, К-7).


						ГД-2026-010-АИ	
						Дом 331 м²	
						Общая площадь 270,67* м² · * размеры приняты, не замерены (реестр — л. 8–10, К-1)	
Изм.	Кол.уч	Лист	№ док.	Подп.	Дата		
Разраб.		Кырлан А.С.			04.11.26	Дизайн-проект интерьера	Стадия: РП; Лист: 25; Листов: 216
Пров.							
ГИП							
						Ведомость заполнения проёмов М б/м	**Кырлан Александр Сергеевич**
Н. контр.							
Утв.							

выпуск 04.11.2026 № 2a77323a49 · стр. 25 из 221


Схемы дверных блоков

Продолжение ведомости заполнения проёмов · вид со стороны открывания · размеры в мм

Схемы дверных блоков (1:40) — вид со стороны открывания; вершина треугольника — сторона петель — продолжение; ведомость и примечания — лист 25

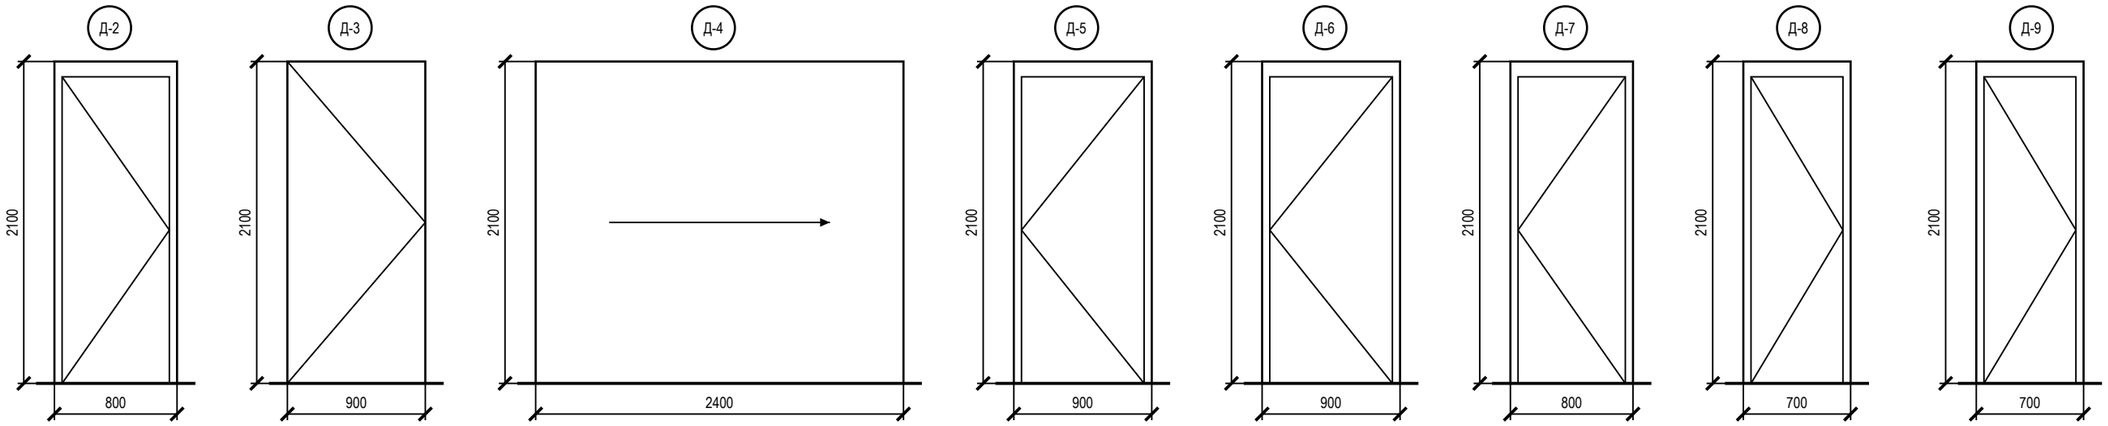

Д-2	Д-3	Д-4	Д-5	Д-6	Д-7	Д-8	Д-9
полотно 700×2000 (расч.) откр. П	блок — по ГОСТ 31173 откр. П	полотно не задано (записи реестра нет) раздвижная	полотно 800×2000 (расч.) откр. Л	полотно 800×2000 (расч.) откр. Л	полотно 700×2000 (расч.) откр. Л	полотно 600×2000 (расч.) откр. П	полотно 600×2000 (расч.) откр. П

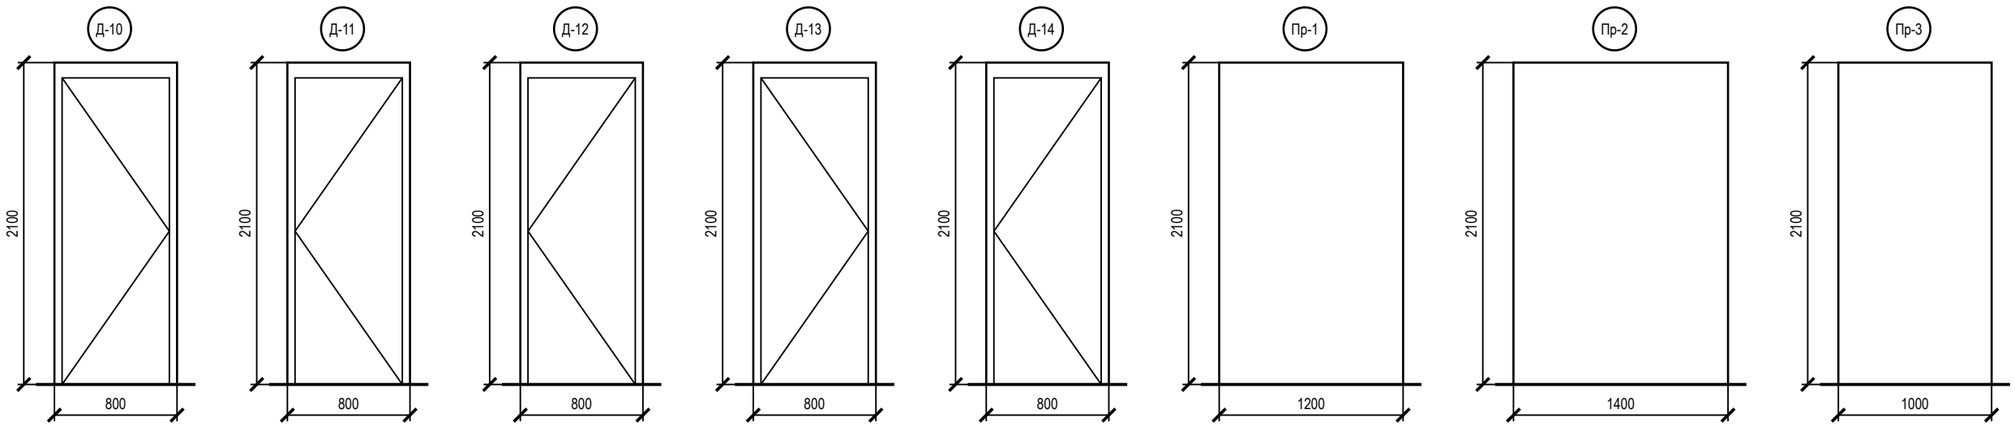

Д-10	Д-11	Д-12	Д-13	Д-14	Пр-1	Пр-2	Пр-3
полотно 700×2000 (расч.) откр. П	полотно 700×2000 (расч.) откр. Л	полотно 700×2000 (расч.) откр. Л	полотно 700×2000 (расч.) откр. П	полотно 700×2000 (расч.) откр. Л	без заполнения	без заполнения	без заполнения

Допущения и предложения на листе

Основа листа: размеры и контуры этажей подобраны проектировщиком по составу помещений и площадям этажей с картинки 470 px (размеры на ней не читаются); обмер и исходный проект — задание (К-1); высоты: 1-й этаж 2800 мм, мансарда 2700 мм (горизонтальная часть) приняты; скаты кровли мансарды приняты по картинке: колено 1200 мм, уклон 45°, конёк вдоль длинной стороны; проект КР — задание (К-2); наружные стены 400 мм, перегородки 120 мм приняты (К-1); разрешённая мощность 15 кВт принята по типовым ТУ для частного дома (К-4); подрайон климата не задан — принят не северный (жилые от 2,5 м) (К-7).

См. лист открытых вопросов (лист 8, записи К-1, К-2, К-4, К-7).

Изм.	Кол.уч	Лист	№ док.	Подп.	Дата
Разраб.		Кырлан А.С.			04.11.26
Пров.					
ГИП					
Н. контр.					
Утв.					

ГД-2026-010-АИ

Дом 331 м²

Общая площадь 270,67* м² · * размеры приняты, не замерены (реестр — л. 8–10, К-1)

Дизайн-проект интерьера

Стадия	Лист	Листов
РП	26	216

Схемы дверных блоков

М б/м

Кырлан Александр Сергеевич


выпуск 04.11.2026 № 2a7732a49 · стр. 26 из 221

Лестница Л-1


План марша, разрез 1-1, узел крепления стойки ограждения, спецификация · отметки от ±0,000 (чистый пол этажа 1) · размеры в мм

ПРЕДВАРИТЕЛЬНО · не для производства работ · открыто пунктов: 15 (реестр — л. 8–10)

План марша Л-1* (М 1:50) · 6. Холл с лестницей

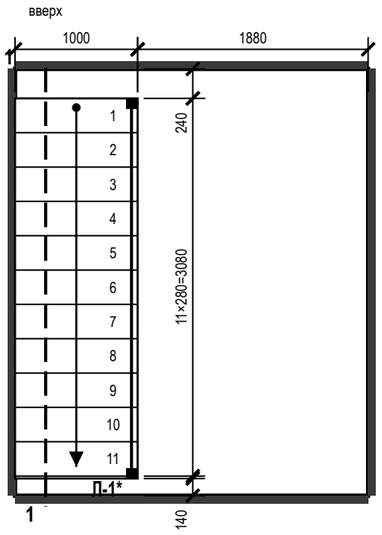


Разрез 1-1 (М 1:50)

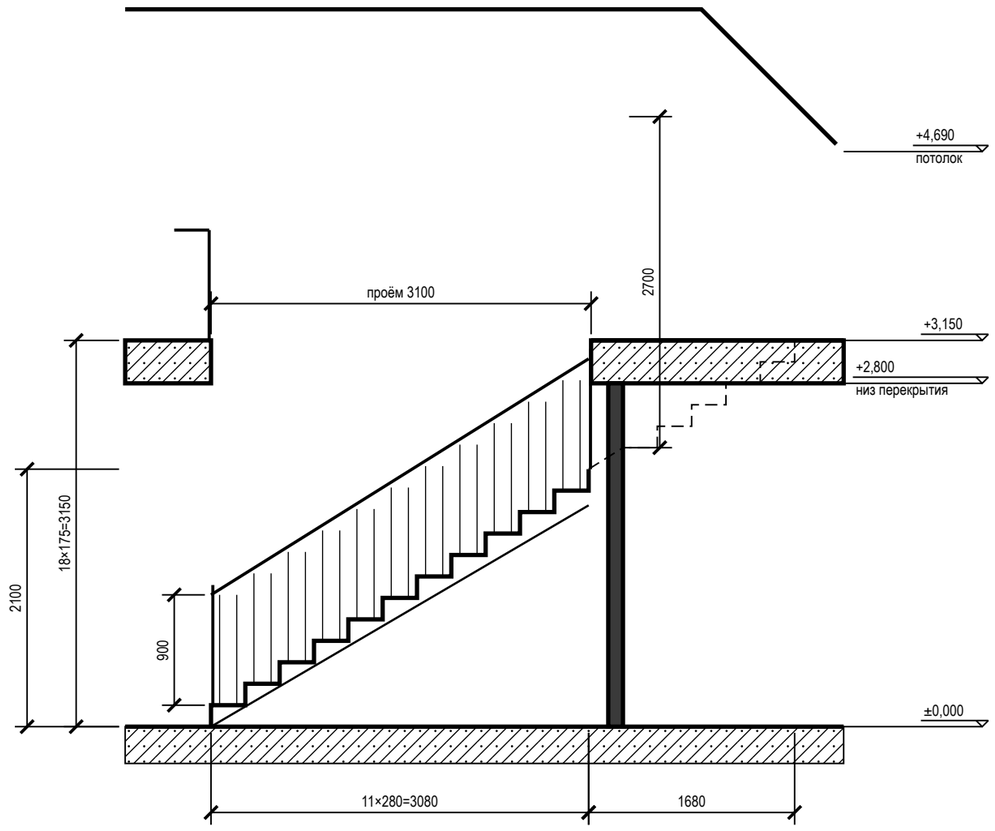

Спецификация элементов лестницы Л-1* — не для заказа

Поз.	Наименование	Кол.	Материал, сечение	Примечание
1	Ступень (проступь)	17	дуб, массив 40 мм, масло	1000×280; на черт. 11
2	Подступенок	18	дуб 18 мм	высота 175; на черт. 12
3	Косоур	2	косоуры стальные 80×40×4, порошковая окраска	несущие марша
4	Столб ограждения марша	2	сталь 20×20, порошковая окраска	по концам марша, стороны Б
5	Балясина	46	сталь 20×20, порошковая окраска	шаг 120, просвет 100
6	Поручень марша	1	дуб 40×60	L ≈ 5,61 м, h 900
7	Столб ограждения проёма	3	сталь 20×20, порошковая окраска	углы проёма, стороны А, Б
8	Балясина ограждения проёма	34	сталь 20×20, порошковая окраска	шаг 120
9	Поручень ограждения проёма	1	дуб 40×60	L ≈ 4,10 м, h 900
10	Крепёж ограждения	1	комплект по изделию	нагрузка на поручень 0,5 кН/м

Узел 1. Крепление стойки ограждения (М 1:5)

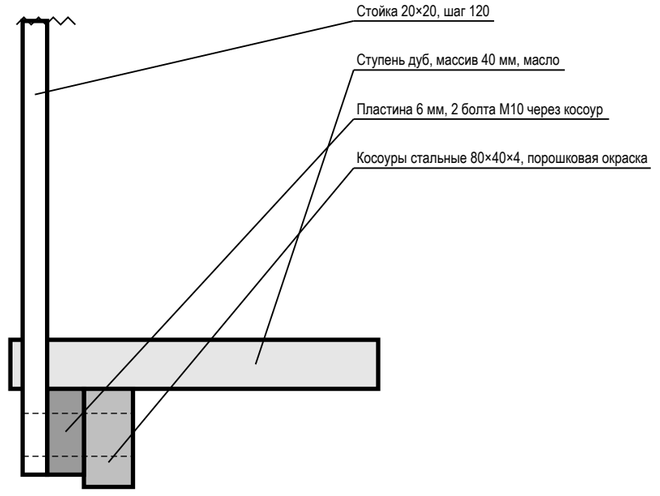

Зазор от низа заполнения до ступени — не более 100 (ГОСТ 25772-2025, прил. А, прим. 3)

Примечания

1. Лестница Л-1*: 18 подъёмов × 175 мм = 3150 мм (отм. ±0,000 … +3,150), проступь 280 мм, ширина марша 1000 мм; уклон 32,0°, шаг 2h + b = 630 мм (удобно 600–640 — практика).
2. В габарит марша 3100 мм входят 11 проступей (до отм. +2,100); до пола этажа выше нужно 17 проступей — 4760 мм (показаны штрихом): одномаршевая лестница в этом помещении не встаёт, решение по реестру (К-6). Спецификация расчёт на марш до пола этажа выше, не для заказа: количества пересчитать после решения по типу лестницы.
3. Ограждение марша со стороны Б: балясины, просвет между элементами 100 мм (не больше 150 — ГОСТ 25772-2025, табл. 3, тип МВ); высота 900 мм, поручень с одной стороны на 900 мм по линии носков (не менее 900 — СП 55.13330.2016, п. 8.3; СП 59.13330.2020, п. 6.2.11).
4. Проём в перекрытии 1000×3100 мм на этаже 2 ограждён со сторон А, Б высотой 900 мм, непрерывно, с поручнем (СП 55.13330.2016, п. 8.3); нагрузка на поручень 0,5 кН/м (СП 20.13330.2016, п. 8.2.6).
5. Просвет над линией носков — не менее 2700 мм (ступень 13, под потолком мансарды); рекомендуется не менее 2000, путь эвакуации — 2200 (СП 55.13330.2016, п. 7.4).
6. Все подступенки одной высоты (СП 55.13330.2016, п. 8.2). Разность отметок чистых полов замерить до заказа изделия: высота подступенка — по замеру.
7. Узел 1 — типовое решение крепления стойки к косоуру; крепёж, сечения и материал — по проекту изделия изготовителя лестницы.

Допущения и предложения на листе

Основа листа: размеры и контуры этажей подобраны проектировщиком по составу помещений и площадям этажей с картинки 470 px (размеры на ней не читаются); обмер и исходный проект — задание (К-1); высоты: 1-й этаж 2800 мм, мансарда 2700 мм (горизонтальная часть) приняты; скаты кровли мансарды приняты по картинке: колено 1200 мм, уклон 45°, конёк вдоль длинной стороны; проект КР — задание (К-2); наружные стены 400 мм, перегородки 120 мм приняты (К-1); разрешённая мощность 15 кВт принята по типовым ТУ для частного дома (К-4); подрайон климата не задан — принят не северный (жилые от 2,5 м) (К-7).

Знак «*» — принято, не замерено и не подтверждено (замерить на объекте): К-6: Л-1 — габарит марша снят с картинки заказчика (11 проступей в холле 3,6 м), а до отм. +3,150 нужно 18 подъёмов — одномаршевая не встаёт: решение по К-6.

См. лист открытых вопросов (лист 8, записи К-1, К-2, К-4, К-6, К-7).

1000 мм · печать 1:1

Изм.	Кол.уч	Лист	№ док.	Подп.	Дата
Разраб.		Кырлан А.С.			04.11.26
Пров.					
ГИП					
Н. контр.					
Утв.					

ГД-2026-010-АИ

Дом 331 м²

Общая площадь 270,67* м² · * размеры приняты, не замерены (реестр — л. 8–10, К-1)

Дизайн-проект интерьера

Стадия	Лист	Листов
РП	27	216

Лестница Л-1

М 1:50

Кырлан Александр Сергеевич

выпуск 04.11.2026 № 2a7323a49 · стр. 27 из 221

Концепция интерьера · 1-й этаж


Шале · схема комплементарная · 60/30/10 · материалы, образы и зонирование

ПРЕДВАРИТЕЛЬНО · не для производства работ · открыто пунктов: 15 (реестр — л. 8–10)


Идея

Стиль — шале: защищённый, тёплый, основательный, природный, камерный, после мороза — у огня. Загородный дом у леса. Стены — шерстяной белый Joa's White No. 226 и молочный S 0804-Y30R, потолки — известковый Slaked Lime No. 105; второй план — выцветший оливковый V451, шалфей S 3020-G30Y, песчаник X463; акценты — хвойный S 7020-G10Y, терракота Red Earth No. 64, брусника Eating Room Red No. 43. Дерево — дуб и лиственница под маслом, камень у камина. Цветовая схема — комплементарная, пропорция 60/30/10: база на стенах и потолках, вторичный цвет — в текстиле и мягкой мебели, акцент — точечно.

Мудборд: материалы и фактуры

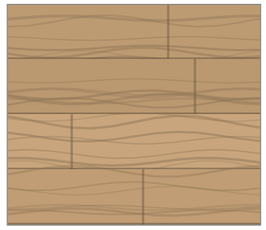

1167-4250
пол

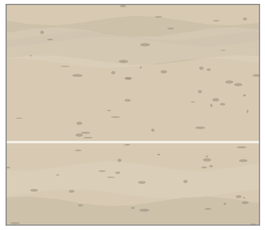

Керамогранит матовый
фартук



Slaked Lime · Little Greene No. 105
потолок, стены, плинтус



Joa's White · Farrow & Ball No. 226
стены, плинтус




NCS S 0804-Y30R
стены, потолок, плинтус




Bancha · Farrow & Ball No. 298
акцент (стена А)



Studio Green — почти чёрный зелёный · Farrow & Ball No. 93
акцент (стена А)

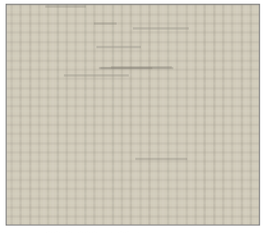

Лён, NCS S 2005-Y20R
Рулонная штора кассетная, Портьеры-волна

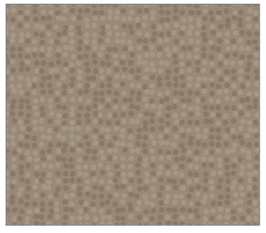

Шерсть, Farrow & Ball No. 40
портьеры на люверсах

Палитра 60/30/10



60 % база — Farrow & Ball No. 226 Joa's White, LRV 63; NCS S 0804-Y30R, LRV 85; Little Greene No. 105 Slaked Lime, LRV 82

30 % вторичный — Tikkurila V451, LRV 51; NCS S 3020-G30Y, LRV 38; Tikkurila X463, LRV 51; Farrow & Ball No. 229 Elephant's Breath — тёплый средне-серый с лиловым подтоном, LRV 52; Farrow & Ball No.

10 % акцент — NCS S 7020-G10Y Хвойный тёмно-зелёный, LRV 5; Farrow & Ball No. 64 Red Earth, LRV 18; Farrow & Ball No. 43 Eating Room Red — брусничный красный, LRV 11.8

Функциональное зонирование (М 1:200)



дневная зона: гостиная, кухня, столовая
мокрая зона: санузлы
хранение: гардеробная, кладовая
вход и коммуникации
(1) номер помещения (лист 30)

Образы помещений

5. Гостиная 33,74 м²
стены NCS S 0804-Y30R; акцент No. 93 на стене

1. Кухня-столовая 24,59 м²
стены NCS S 0804-Y30R

2. Кабинет-гостевая 11,92 м²
стены Farrow & Ball No. 226; акцент No. 298 на

8. Прихожая 12,46 м²
стены Farrow & Ball No. 226

9. Тамбур 3,49 м²
стены Farrow & Ball No. 226

6. Холл с лестницей 10,02 м²
стены Farrow & Ball No. 226

3. Санузел 1 этажа 4,87 м²
стены Atlas Concorde A8UZ

4. Котельная 6,88 м²
стены Farrow & Ball No. 226

7. Кладовая 5,99 м²
стены Little Greene No. 105

10. Гараж 41,58 м²
стены Farrow & Ball No. 226

11. Веранда 21,84 м²
стены NCS S 0804-Y30R

12. Крыльцо 3,38 м²
стены NCS S 0804-Y30R

Материалы и отделка

1167-4250
пол — пом. 1, 2, 5, 6, 7

Керамогранит матовый
тон F497; 600×600
фартук — пом. 1

Керамогранит ректифицированный под травертин
матовый; 600×600
пол — пом. 3

A8UZ
стены, пол — пом. 3, 4, 8, 9, 11, 12

Плинтус из керамогранита пола
подрезка 80 мм, верхняя кромка с запилом 45°
плинтус — пом. 11, 12

NCS S 0804-Y30R, LRV 85
Tikkurila Luja 7
стены, потолок, плинтус — пом. 1, 5, 11, 12

Farrow & Ball No. 226 Joa's White, LRV 63
Farrow & Ball Modern Emulsion, матовая
стены, плинтус — пом. 2, 4, 6, 8, 9, 10

Little Greene No. 105 Slaked Lime, LRV 82
Little Greene Absolute Matt, глубокоматовая
потолок, стены, плинтус — пом. 2, 3, 4, 6, 7, 8, 9, 10

Farrow & Ball No. 298 Bancha, LRV 14
акцентная стена
акцент (стена А) — пом. 2

Текстиль и металл

Лён, NCS S 2005-Y20R
Рулонная штора кассетная, Портьеры-волна

Шерсть, Farrow & Ball No. 40
портьеры на люверсах

Вуаль, NCS S 0804-Y30R
тюль, Тюль-вуаль

Шерсть, Tikkurila X463
ковёр джутовый под диваном

Лён, NCS S 3010-Y30R
подушки на диван

Бархат, Farrow & Ball No. 298
подушки на кровать

Шерсть, Farrow & Ball No. 298
плед на кровать

Шерсть, Farrow & Ball No. 243
ковёр мягкой группы

Лён, Farrow & Ball No. 226
подушки декоративные на диван

Бархат, Farrow & Ball No. 93
Подушки декоративные на диван

Чего избегаем

1) Эффект сауны: сосна под оранжевым лаком на стенах, потолке и полу одновременно
2) Тёмное дерево в низкой комнате без светлого потолка
3) Пластиковые/полиуретановые балки с повторяющимся рисунком
4) Избыток трофеев, рогов и шкур — охотничий домик
5) Заставленность альпийскими сувенирами
6) Холодный свет и много точек в потолке

Допущения и предложения на листе

Основа листа: размеры и контуры этажей подобраны проектировщиком по составу помещений и площадям этажей с картинки 470 px (размеры на ней не читаются); обмер и исходный проект — задание (К-1); высоты: 1-й этаж 2800 мм, мансарда 2700 мм (горизонтальная часть) приняты; скаты кровли мансарды приняты по картинке: колено 1200 мм, уклон 45°, конёк вдоль длинной стороны; проект КР — задание (К-2); наружные стены 400 мм, перегородки 120 мм приняты (К-1); разрешённая мощность 15 кВт принята по типовым ТУ для частного дома (К-4); подрайон климата не задан — принят не северный (жилые от 2,5 м) (К-7).
См. лист открытых вопросов (лист 8, записи К-1, К-2, К-4, К-7).

Примечания

1. Коды цвета — по веерам производителей (колерная карта, лист 95); перед закупкой краски — выкрас на стене объекта под дневным светом и лампами проекта.
2. Материалы — по ведомости отделки (лист 91); мебель, текстиль и декор — по спецификации (лист 32). Образцы доски, керамогранита и тканей утвердить до заказа.
3. Фактуры на листе условные, цвет передан по HEX-значениям производителей: при печати возможны отклонения, решение — только по физическому образцу.

Изм.	Кол.уч	Лист	№ док.	Подп.	Дата
Разраб.		Кырлан А.С.			04.11.26
Пров.					
ГИП					
Н. контр.					
Утв.					

ГД-2026-010-АИ

Дом 331 м²

Общая площадь 270,67* м² · * размеры приняты, не замерены (реестр — л. 8–10, К-1)

Дизайн-проект интерьера

Стадия	Лист	Листов
РП	28	216

Концепция интерьера · 1-й этаж

М б/м

Кырлан Александр Сергеевич

выпуск 04.11.2026 № 2a77323a49 · стр. 28 из 221

Концепция интерьера · Мансарда


Шале · схема комплементарная · 60/30/10 · материалы, образы и зонирование

ПРЕДВАРИТЕЛЬНО · не для производства работ · открыто пунктов: 15 (реестр — л. 8–10)


Идея

Стиль — шале: защищённый, тёплый, основательный, природный, камерный, после мороза — у огня. Загородный дом у леса. Стены — шерстяной белый Joa's White No. 226 и молочный S 0804-Y30R, потолки — известковый Slaked Lime No. 105; второй план — выцветший оливковый V451, шалфей S 3020-G30Y, песчаник X463; акценты — хвойный S 7020-G10Y, терракота Red Earth No. 64, брусника Eating Room Red No. 43. Дерево — дуб и лиственница под маслом, камень у камина. Цветовая схема — комплементарная, пропорция 60/30/10: база на стенах и потолках, вторичный цвет — в текстиле и мягкой мебели, акцент — точечно.

Мудборд: материалы и фактуры

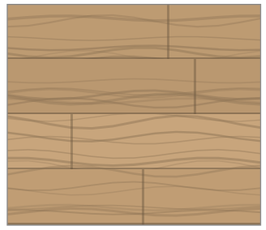

1167-4250
пол

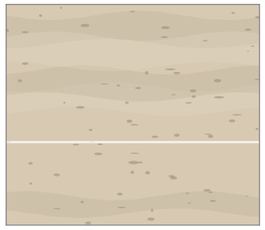

Керамогранит ректифицированный под травертин
пол



Slaked Lime · Little Greene No. 105
потолок, стены, плинтус



Joa's White · Farrow & Ball No. 226
стены, плинтус



Хвойный тёмно-зелёный · NCS S 7020-G10Y
акцент (стена А)




Red Earth · Farrow & Ball No. 64
акцент (стена А)



NCS S 3020-G30Y
акцент (стена А)



NCS S 3040-Y70R
акцент (стена А)

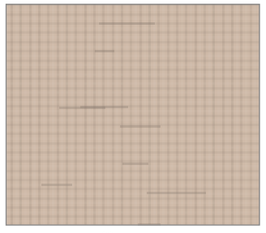

Лён, Tikkurila X463
портьеры-волна, подушки декоративные на кровать

Палитра 60/30/10



60 % база — Farrow & Ball No. 226 Joa's White, LRV 63; NCS S 0804-Y30R, LRV 85; Little Greene No. 105 Slaked Lime, LRV 82

30 % вторичный — Tikkurila V451, LRV 51; NCS S 3020-G30Y, LRV 38; Tikkurila X463, LRV 51; Farrow & Ball No. 229 Elephant's Breath — тёплый средне-серый с лиловым подтоном, LRV 52; Farrow & Ball No.

10 % акцент — NCS S 7020-G10Y Хвойный тёмно-зелёный, LRV 5; Farrow & Ball No. 64 Red Earth, LRV 18; Farrow & Ball No. 43 Eating Room Red — брусничный красный, LRV 11.8

Функциональное зонирование (М 1:200)



ночная зона: спальни
хранение: гардеробная, кладовая
(1) номер помещения (лист 30)
мокрая зона: санузлы
вход и коммуникации

Образы помещений

13. Спальня мастер — 24,59 м²



стены Farrow & Ball No. 226; акцент S 7020-G10Y на стене А
пол — 1167-4250
текстиль: портьеры No. 229, тюль No. 105, ковёр S 2005-Y20R

16. Спальня 2 — 15,52 м²



стены Farrow & Ball No. 226; акцент No. 64 на стене А
пол — 1167-4250
текстиль: портьеры X463, тюль No. 105, ковёр S 3010-Y30R

18. Спальня 3 — 17,11 м²



стены Farrow & Ball No. 226; акцент S 3020-G30Y на стене А
пол — 1167-4250
текстиль: портьеры на люверсах V451, тюль S 0804-Y30R, ковёр S 2005-Y20R

19. Спальня 4 — 16,28 м²



стены Farrow & Ball No. 226; акцент S 3040-Y70R на стене А
пол — 1167-4250
текстиль: портьеры S 2005-Y20R, тюль No. 226, ковёр S 3010-Y30R

17. Холл мансарды — 21,72 м²



стены Farrow & Ball No. 226
пол — 1167-4250
текстиль: коврик для йоги и растяжки 1830×610×6 S 3020-G30Y
декор: Монстера в кашпо

14. Гардеробная мастер — 6,74 м²



стены Little Greene No. 105
пол — 1167-4250
свет 3000 K

15. Санузел мастер — 6,88 м²



стены Atlas Concorde A8UZ
пол — керамогранит под травертин, матовый
свет 3000 K

20. Санузел 2 — 6,29 м²



стены Atlas Concorde A8UZ
пол — керамогранит под травертин, матовый
свет 3000 K

Материалы и отделка



1167-4250
пол — пом. 13, 14, 16, 17, 18, 19



Керамогранит ректифицированный под травертин
матовый; 600×600
пол — пом. 15, 20



A8UZ
стены — пом. 15, 20



Farrow & Ball No. 226 Joa's White, LRV 63
Farrow & Ball Modern Emulsion, матовая
стены, плинтус — пом. 13, 16, 17, 18, 19



Little Greene No. 105 Slaked Lime, LRV 82
Little Greene Absolute Matt, глубокоматовая
потолок, стены, плинтус — пом. 13, 14, 15, 16, 17, 18, 19, 20



NCS S 7020-G10Y Хвойный тёмно-зелёный, LRV 5
акцентная стена
акцент (стена А) — пом. 13



Farrow & Ball No. 64 Red Earth, LRV 18
акцентная стена
акцент (стена А) — пом. 16



NCS S 3020-G30Y, LRV 38
акцентная стена
акцент (стена А) — пом. 18



NCS S 3040-Y70R, LRV 24
акцентная стена
акцент (стена А) — пом. 19

Текстиль и металл



Шерсть, Farrow & Ball No. 229
портьеры-волна



Шерсть, NCS S 2005-Y20R
ковёр под кроватью, подушки декоративные на кровать



Шерсть, NCS S 7020-G10Y
плед на кровать



Шерсть, NCS S 3010-Y30R
ковёр под кроватью



Шерсть, Farrow & Ball No. 64
плед на кровать



Вуаль, Little Greene No. 105
тюль



Бархат, NCS S 7020-G10Y
подушки на кровать



Лён, Tikkurila X463
портьеры-волна, подушки декоративные на кровать



Бархат, Farrow & Ball No. 64
подушки на кровать



Чёрный матовый металл
зеркало в рост, зеркало безопасное

Чего избегаем

1) Эффект сауны: сосна под оранжевым лаком на стенах, потолке и полу одновременно
2) Тёмное дерево в низкой комнате без светлого потолка
3) Пластиковые/полиуретановые балки с повторяющимся рисунком
4) Избыток трофеев, рогов и шкур — охотничий домик
5) Заставленность альпийскими сувенирами
6) Холодный свет и много точек в потолке

Допущения и предложения на листе. Основа листа: размеры и контуры этажей подобраны проектировщиком по составу помещений и площадям этажей с картинки 470 px (размеры на ней не читаются); обмер и исходный проект — задание (К-1); высоты: 1-й этаж 2800 мм, мансарда 2700 мм (горизонтальная часть) приняты; скаты кровли мансарды приняты по картинке: колено 1200 мм, уклон 45°, конёк вдоль длинной стороны; проект КР — задание (К-2); наружные стены 400 мм, перегородки 120 мм приняты (К-1); разрешённая мощность 15 кВт принята по типовым ТУ для частного дома (К-4); подрайон климата не задан — принят не северный (жилые от 2,5 м) (К-7). Знак «*» — принято, не замерено и не подтверждено (замерить на объекте): К-2: отметка чистого пола этажа «Мансарда» +3,150 — принята без источника, все отметки мансарды считаются от неё. См. лист открытых вопросов (лист 8, записи К-1, К-2, К-4, К-7).

Примечания


1. Коды цвета — по веерам производителей (колерная карта, лист 95); перед закупкой краски — выкрас на стене объекта под дневным светом и лампами проекта.
2. Материалы — по ведомости отделки (лист 91); мебель, текстиль и декор — по спецификации (лист 32). Образцы доски, керамогранита и тканей утвердить до заказа.
3. Фактуры на листе условные, цвет передан по HEX-значениям производителей: при печати возможны отклонения, решение — только по физическому образцу.

						ГД-2026-010-АИ	
						Дом 331 м²	
						Общая площадь 270,67* м² · * размеры приняты, не замерены (реестр — л. 8–10, К-1)	
Изм.	Кол.уч	Лист	№ док.	Подп.	Дата	Дизайн-проект интерьера	Стадия: РП; Лист: 29; Листов: 216
Разраб.		Кырлан А.С.			04.11.26	Концепция интерьера · Мансарда	Кырлан Александр Сергеевич
Пров.						М б/м	
ГИП							
Н. контр.							
Утв.							

выпуск 04.11.2026 № 2a77323a49 · стр. 29 из 221

План расстановки мебели · 1-й этаж

Мебель и оборудование · размеры в мм от чистовых стен · марки — по ведомости

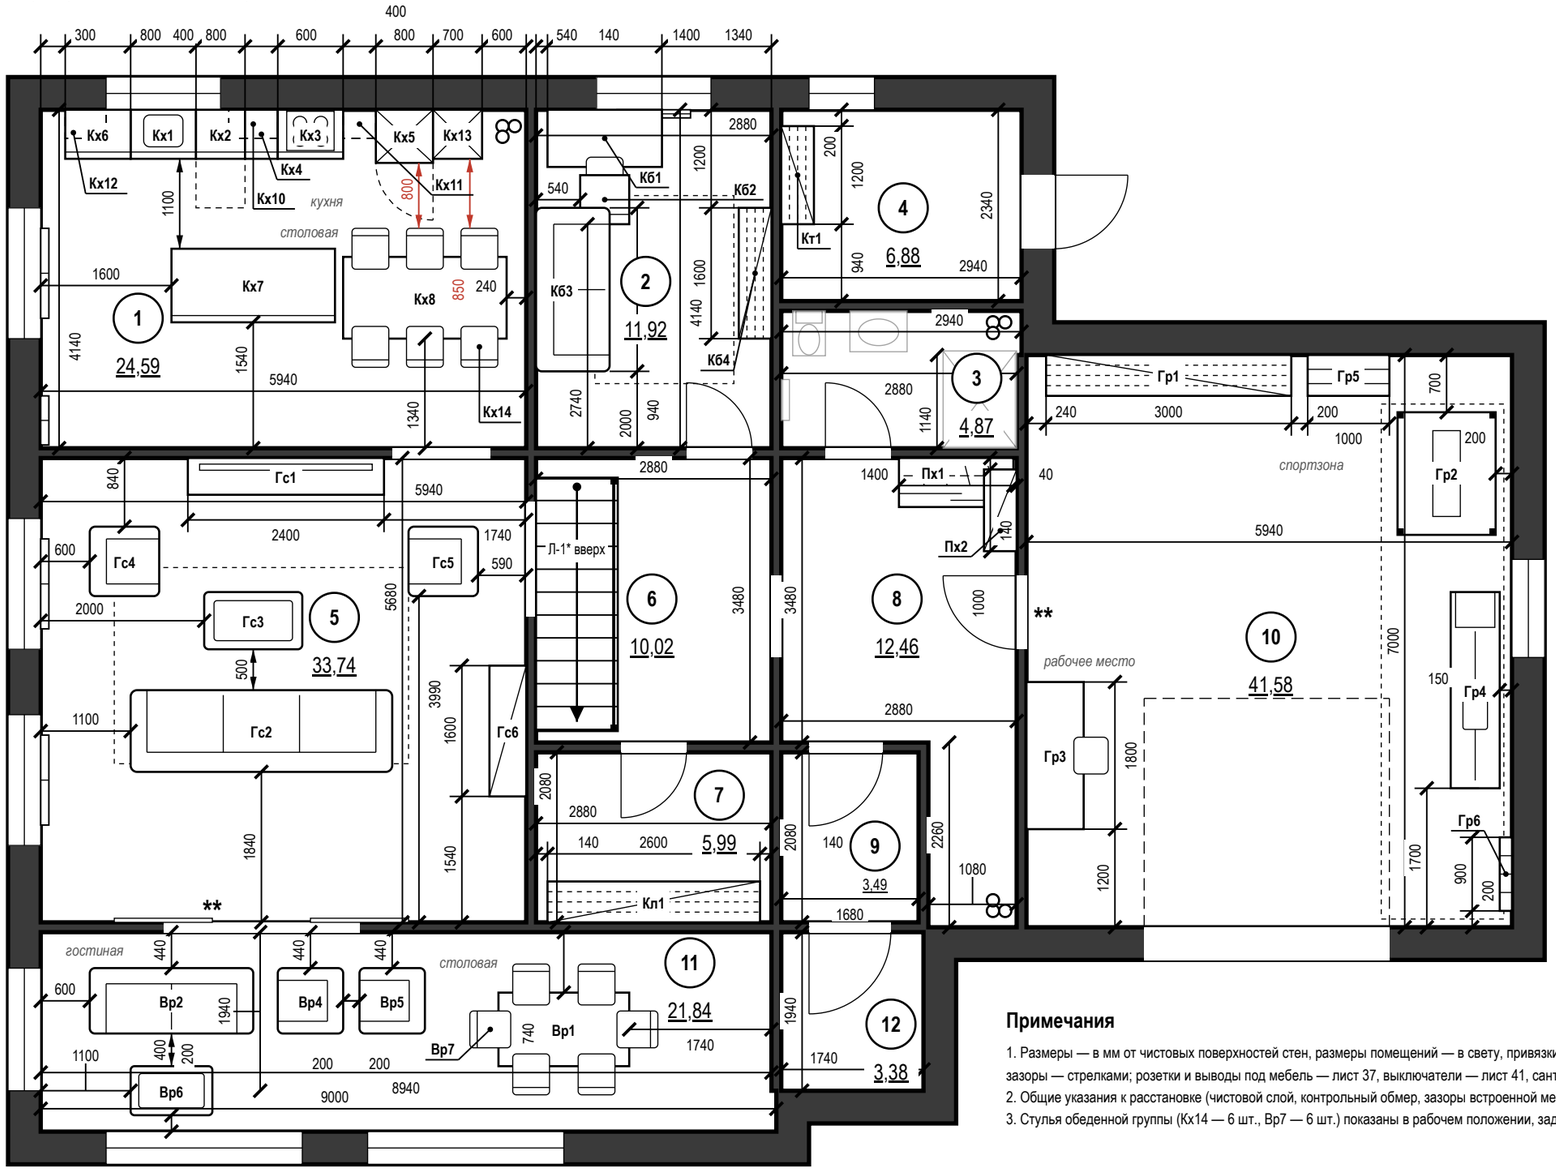

Экспликация помещений

лист 19 · на плане — номера в марках

Ведомость мебели и оборудования

39 позиц. (49 шт.) — не помещается на листе:
полностью на листе 32 «Спецификация мебели и оборудования»
марка, наименование, Ш×Г×В, материал, модель,
допуск замены. Марки на плане — по ней.

Условные обозначения

- мебель и оборудование — габарит в масштабе
- навесные шкафы (низ выше 0,9 м) — невидимый контур
- ковёр
- зона открывания дверец шкафов и техники
- К1 — марка предмета по ведомости мебели
- привязка от чистовой стены, мм
- ширина прохода, зазор, мм
- проход меньше нормы — расстановку изменить
- сантехприборы — подложка (лист ВК)
- радиатор отопления (лист ОВ)
- существующие стены (сечение)
- ** — «**» — предложение проектировщика, заказчиком не утверждено
- стояк: К1 — канализация, В1 — ХВС, Т3 — ГВС
- 1 — номер помещения, площадь м²
- *зона* — функциональная зона помещения

Примечания

1. Размеры — в мм от чистовых поверхностей стен, размеры помещений — в свету, привязки — от стен, углов помещения и соседних предметов, проходы и зазоры — стрелками; розетки и выводы под мебель — лист 37, выключатели — лист 41, сантехприборы — лист 56.
2. Общие указания к расстановке (чистовой слой, контрольный обмер, зазоры встроенной мебели, замена покупной) — примечания к спецификации, лист 32.
3. Стулья обеденной группы (Кх14 — 6 шт., Вр7 — 6 шт.) показаны в рабочем положении, задвинутыми под столешницу на 150 мм.

Допущения и предложения на листе

Основа листа: размеры и контуры этажей подобраны проектировщиком по составу помещений и площадям этажей с картинки 470 px (размеры на ней не читаются); обмер и исходный проект — задание (К-1); высоты: 1-й этаж 2800 мм, мансарда 2700 мм (горизонтальная часть) приняты; скаты кровли мансарды приняты по картинке: колено 1200 мм, уклон 45°, конёк вдоль длинной стороны; проект КР — задание (К-2); наружные стены 400 мм, перегородки 120 мм приняты (К-1); разрешённая мощность 15 кВт принята по типовым ТУ для частного дома (К-4); подрайон климата не задан — принят не северный (жилые от 2,5 м) (К-7).

Знак «*» — принято, не замерено и не подтверждено (замерить на объекте): К-6: Л-1 — габарит марша снят с картинки заказчика (11 проступей в холле 3,6 м), а до отм. +3,150 нужно 18 подъёмов — одномаршевая не встаёт: решение по К-6.

Знак «**» — предложение проектировщика, заказчиком не утверждено (согласовать с заказчиком): дверь пом. 8 (стена Б) — дверь гаража в дом — СП 55.13330.2016 п. 7.7: EI 30, уплотнение в притворах, самозакрывание (доводчик); К-9: дверь пом. 5 (стена В) — проём 2400×2100 на веранду с картинки: одной распашной створкой не закрывается (полотна 600–900) — раздвижная двустворчатая, остеклённая; система и полотна — по каталогу после утверждения автором.

Открытые вопросы и конфликты по листу: К-1, К-9, Кф-1.

Изменения по листу без подписи: ИЗ-2.

См. лист открытых вопросов (лист 8, записи К-1, К-2, К-4, К-6, К-7; лист 9, запись К-9; лист 10, записи ИЗ-2, Кф-1).

1000 мм · печать 1:1

Изм.	Кол.уч	Лист	№ док.	Подп.	Дата
Разраб.		Кырлан А.С.			04.11.26
Пров.					
ГИП					
Н. контр.					
Утв.					

ГД-2026-010-АИ

Дом 331 м²

Общая площадь 270,67* м² · * размеры приняты, не замерены (реестр — л. 8–10, К-1)

Дизайн-проект интерьера

Стадия	Лист	Листов
РП	30	216


План расстановки мебели · 1-й этаж

М 1:75

Кырлан Александр Сергеевич

План расстановки мебели · Мансарда

Мебель и оборудование · размеры в мм от чистовых стен · марки — по ведомости

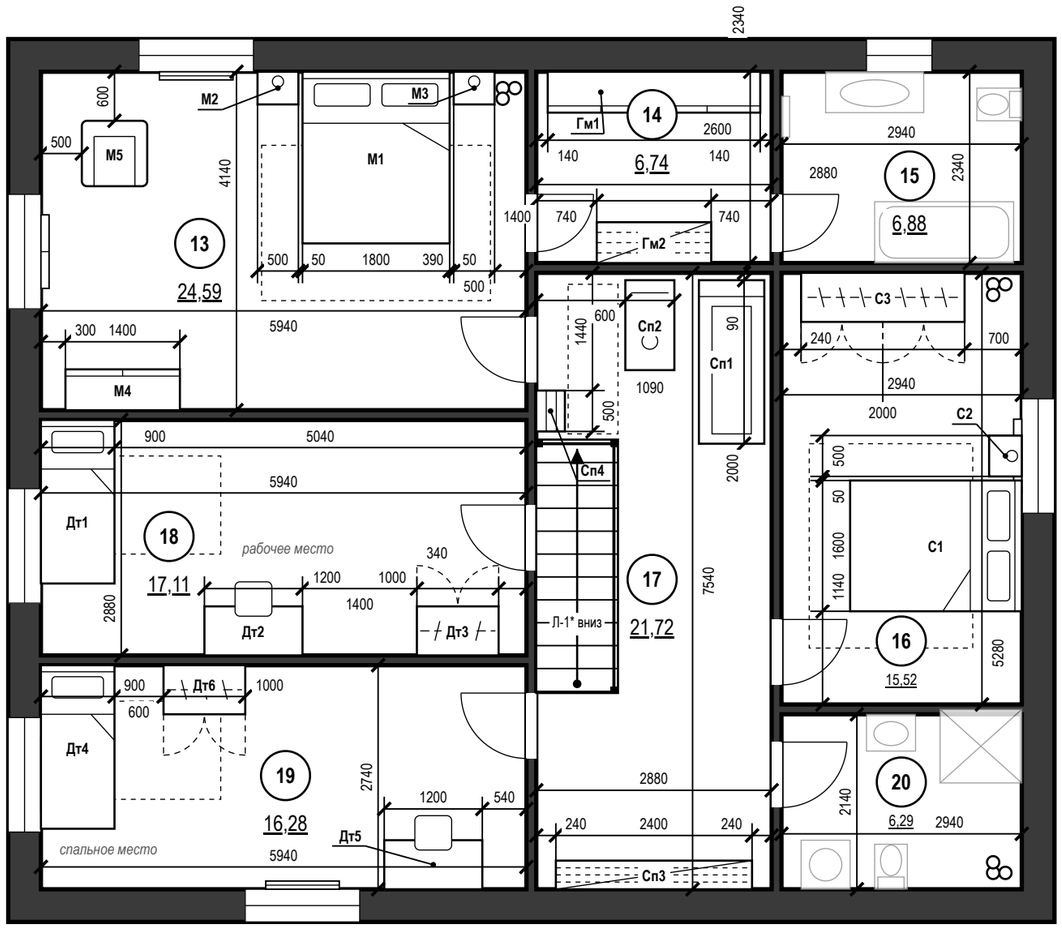

Примечания

1. Размеры — в мм от чистовых поверхностей стен, размеры помещений — в свету, привязки — от стен, углов помещения и соседних предметов; розетки и выводы под мебель — лист 38, выключатели — лист 42, сантехприборы — лист 57.
2. Общие указания к расстановке (чистовой слой, контрольный обмер, зазоры встроенной мебели, замена покупной) — примечания к спецификации, лист 32.
3. Отступ от стены, на плане не образмерен: Сп1 — 90 мм, Сп2 — 90 мм.

Экспликация помещений

лист 20 · на плане — номера в марках

Ведомость мебели и оборудования

Марка	Наименование	Ш×Г×В, мм	Пом.	Кол.
М1	Кровать 1800×2000	1800×2100×450	13	1
М2	Тумба прикроватная	500×400×550	13	1
М3	Тумба прикроватная	500×400×550	13	1
М4	Комод	1400×500×800	13	1
М5	Кресло для чтения	800×800×900	13	1
Гм1	Ящики низкие под скатом	2600×500×1100	14	1
Гм2	Система хранения открытая	1400×500×2400	14	1
С1	Кровать 1600×2000	1600×2100×450	16	1
С2	Тумба подвесная	500×400×550	16	1
С3	Шкаф распашной	2000×600×2400	16	1
Сп1	Дорожка беговая складная	2000×800×1400	17	1
Сп2	Велотренажёр магнитный	600×1100×1150	17	1
Сп3	Стеллаж низкий под скатом	2400×350×900	17	1
Сп4	Стойка-этажерка для инвентаря	500×350×1000	17	1
Дт1	Кровать 900×2000 с бортиком	900×2000×450	18	1
Дт2	Стол письменный	1200×600×750	18	1
Дт3	Шкаф распашной	1000×600×2200	18	1
Дт4	Кровать 900×2000 с ящиками	900×2000×450	19	1
Дт5	Стол письменный растущий	1200×600×750	19	1
Дт6	Шкаф распашной	1000×600×2200	19	1

Ш — вдоль стены (изголовья), Г — от стены (длина кровати)

Материалы, модели, допуск замены — лист 32

Условные обозначения

- мебель и оборудование — габарит в масштабе
- ковёр
- зона открывания дверец шкафов и техники
- К1 — марка предмета по ведомости мебели
- привязка от чистовой стены, мм
- сантехприборы — подложка (лист ВК)
- радиатор отопления (лист ОВ)
- существующие стены (сечение)
- стояк: К1 — канализация, В1 — ХВС, Т3 — ГВС
- 1 — номер помещения, площадь м²
- *зона* — функциональная зона помещения

Допущения и предложения на листе

Основа листа: размеры и контуры этажей подобраны проектировщиком по составу помещений и площадям этажей с картинки 470 px (размеры на ней не читаются); обмер и исходный проект — задание (К-1); высоты: 1-й этаж 2800 мм, мансарда 2700 мм (горизонтальная часть) приняты; скаты кровли мансарды приняты по картинке: колено 1200 мм, уклон 45°, конёк вдоль длинной стороны; проект КР — задание (К-2); наружные стены 400 мм, перегородки 120 мм приняты (К-1); разрешённая мощность 15 кВт принята по типовым ТУ для частного дома (К-4); подрайон климата не задан — принят не северный (жилые от 2,5 м) (К-7).

Знак «*» — принято, не замерено и не подтверждено (замерить на объекте): К-2: отметка чистого пола этажа «Мансарда» +3,150 — принята без источника, все отметки мансарды считаются от неё; К-6: Л-1 — габарит марша снят с картинки заказчика (11 проступей в холле 3,6 м), а до отм. +3,150 нужно 18 подъёмов — одномаршевая не встаёт: решение по К-6.

Открытые вопросы и конфликты по листу: К-1, К-9, Кф-1.

Изменения по листу без подписи: ИЗ-2.

См. лист открытых вопросов (лист 8, записи К-1, К-2, К-4, К-6, К-7; лист 9, запись К-9; лист 10, записи ИЗ-2, Кф-1).

1000 мм · печать 1:1

Изм.	Кол.уч	Лист	№ док.	Подп.	Дата
Разраб.		Кырлан А.С.			04.11.26
Пров.					
ГИП					
Н. контр.					
Утв.					

ГД-2026-010-АИ

Дом 331 м²

Общая площадь 270,67* м² · * размеры приняты, не замерены (реестр — л. 8–10, К-1)

Дизайн-проект интерьера

Стадия	Лист	Листов
РП	31	216

План расстановки мебели · Мансарда

М 1:75

Кырлан Александр Сергеевич

выпуск 04.11.2026 № 2a77323a49 · стр. 31 из 221

01

Планировочное решение

Кырлан Александр Сергеевич

выпуск 04.11.2026 · 2a7323a49 · стр. 32 из 221

Спецификация мебели и оборудования

ПРЕДВАРИТЕЛЬНО · не для производства работ · открыто пунктов: 15 (реестр — л. 8–10)

Форма 1 ГОСТ 21.110-2013 · позиции мебели — по плану расстановки

Поз.	Наименование и техническая характеристика	Тип, марка, обозначение документа, опросного листа	Код продукции	Поставщик	Ед. измерения	Кол.	Масса 1 ед., кг	Примечание
	Мебель встроенная и корпусная (изготовление по чертежам мебельщика)							
Кх1	Модуль под мойку у окна; корпус ЛДСП 16 мм; фасады — МДФ 18 мм, эмаль матовая; цвет фасадов — в цвет стен (NCS S 0804-Y30R); Ш×Г×В 800×600×900 мм			изготовление на заказ	шт.	1		пом. 1
Кх2	Модуль под встраиваемую ПММ 60; без корпуса (ниша между соседними модулями); фасад на дверь машины — МДФ 18 мм, эмаль матовая; цоколь; цвет фасадов — в цвет стен (NCS S 0804-Y30R); Ш×Г×В 600×600×900 мм			изготовление на заказ	шт.	1		пом. 1
Кх3	Модуль с варочной панелью и духовым шкафом; корпус ЛДСП 16 мм; фасады — МДФ 18 мм, эмаль матовая; цвет фасадов в цвет стен (NCS S 0804-Y30R); Ш×Г×В 800×600×900 мм			изготовление на заказ	шт.	1		пом. 1
Кх4	Модуль с ящиками; корпус ЛДСП 16 мм; фасады — МДФ 18 мм, эмаль матовая; цвет фасадов — в цвет стен (NCS S 0804-Y30R); Ш×Г×В 400×600×900 мм			изготовление на заказ	шт.	1		пом. 1
Кх5	Колонна с холодильником; корпус ЛДСП 16 мм; фасады — МДФ 18 мм, эмаль матовая; цвет фасадов — в цвет стен (NCS S 0804-Y30R); Ш×Г×В 700×650×2200 мм			изготовление на заказ	шт.	1		пом. 1
Кх6	Модуль с ящиками; корпус ЛДСП 16 мм; фасады — МДФ 18 мм, эмаль матовая; цвет фасадов — в цвет стен (NCS S 0804-Y30R); Ш×Г×В 800×600×900 мм			изготовление на заказ	шт.	1		пом. 1
Кх7	Остров с барной консолью из массива дуба, столешница — кварц; корпус ЛДСП 16 мм; фасады — МДФ 18 мм, эмаль матовая; цвет фасадов — в цвет стен (NCS S 0804-Y30R); Ш×Г×В 2000×900×900 мм			изготовление на заказ	шт.	1		пом. 1
Кх10	Навесной шкаф, фасад в тон острова; корпус ЛДСП 16 мм; фасады — МДФ 18 мм, эмаль матовая; цвет фасадов — в цвет стен (NCS S 0804-Y30R); Ш×Г×В 600×350×900 мм			изготовление на заказ	шт.	1		пом. 1
Кх11	Навесной шкаф узкий, полки для специй; корпус ЛДСП 16 мм; фасады — МДФ 18 мм, эмаль матовая; цвет фасадов — в цвет стен (NCS S 0804-Y30R); Ш×Г×В 400×350×900 мм			изготовление на заказ	шт.	1		пом. 1
Кх12	Полки открытые из массива дуба у окна, 3 яруса; корпус ЛДСП 16 мм; фасады — МДФ 18 мм, эмаль матовая; цвет фасадов — в цвет стен (NCS S 0804-Y30R); Ш×Г×В 500×350×900 мм			изготовление на заказ	шт.	1		пом. 1
Кх13	Пенал-кладовая с выдвижными корзинами; корпус ЛДСП 16 мм; фасады — МДФ 18 мм, эмаль матовая; цвет фасадов — в цвет стен (NCS S 0804-Y30R); Ш×Г×В 600×600×2200 мм			изготовление на заказ	шт.	1		пом. 1
Кт1	Стеллаж технический; каркас и полки — ЛДСП 16 мм, декор «дуб натуральный»; без фасадов; Ш×Г×В 1200×400×2000 мм			изготовление на заказ	шт.	1		пом. 4
Кл1	Стеллаж для хранения; каркас и полки — ЛДСП 16 мм, декор «дуб натуральный»; без фасадов; Ш×Г×В 2600×500×2200 мм			изготовление на заказ	шт.	1		пом. 7
Пх1	Шкаф-купе, светлый дуб; корпус ЛДСП 16 мм; фасады — ЛДСП 10 мм в алюминиевом профиле; Ш×Г×В 1400×600×2600 мм			изготовление на заказ	шт.	1		пом. 8
Гр1	Стеллаж для инструмента и шин; каркас и полки — ЛДСП 16 мм, декор «дуб натуральный»; без фасадов; Ш×Г×В 3000×500×2000 мм			изготовление на заказ	шт.	1		пом. 10; крепление к стене
Гм2	Система хранения открытая в полную высоту (у перегородки, вне ската); каркас и полки — ЛДСП 16 мм, декор «дуб натуральный»; без фасадов; Ш×Г×В 1400×500×2400 мм			изготовление на заказ	шт.	1		пом. 14
С3	Шкаф распашной, фасады — шпон ясеня с вертикальной рейкой; корпус ЛДСП 16 мм; фасады — МДФ 18 мм, эмаль матовая; цвет фасадов — в цвет стен (Farrow & Ball No. 226); Ш×Г×В 2000×600×2400 мм			изготовление на заказ	шт.	1		пом. 16
Сп3	Стеллаж низкий под скатом для книг и инвентаря; каркас и полки — ЛДСП 16 мм, декор «дуб натуральный»; без фасадов; Ш×Г×В 2400×350×900 мм			изготовление на заказ	шт.	1		пом. 17; крепление к стене
Дт3	Шкаф распашной, фасады — матовая эмаль шалфей; корпус ЛДСП 16 мм; фасады — МДФ 18 мм, эмаль матовая; цвет фасадов — в цвет стен (Farrow & Ball No. 226); Ш×Г×В 1000×600×2200 мм			изготовление на заказ	шт.	1		пом. 18
Дт6	Шкаф распашной (вне ската), фасады — дуб и эмаль терракота; корпус ЛДСП 16 мм; фасады — МДФ 18 мм, эмаль матовая; цвет фасадов — в цвет стен (Farrow & Ball No. 226); Ш×Г×В 1000×600×2200 мм			изготовление на заказ	шт.	1		пом. 19
	Мебель покупная							
Кх8	Стол обеденный 2000×1000, массив дуба; шпон, дуб натуральный, матовое масло; Ш×Г×В 2000×1000×750 мм			аналог по характеристикам	шт.	1		пом. 1; замена ≤ габарита
Кх14	Стул обеденный к столу Кх8; обивка — ткань, цвет Tikkurila V451; каркас — дуб натуральный; Ш×Г×В 450×500×820 мм			аналог по характеристикам	шт.	6		пом. 1; замена ≤ габарита

Примечания

1. Позиции мебели совпадают с марками на плане расстановки (лист 30); размеры Ш×Г×В — Ш вдоль стены, Г от стены.
2. Размеры и привязки плана расстановки — в мм от чистовых поверхностей стен: слой штукатурки 20 мм по блоку и 5 мм шпаклёвки по ГКЛ учтён; привязки — от стен и углов помещения, а не от другой мебели.
3. План расстановки не является документацией для изготовления мебели. Встроенная и корпусная мебель изготавливается по чертежам мебельщика после контрольного обмера (после штукатурки); «стена в стену» — с зазором 10 мм с каждой стороны или с компенсаторами; графы «Тип, марка» и «Код продукции» для неё не заполняются (ГОСТ 21.110-2013).
4. Покупные изделия — аналог по характеристикам: заменять только на изделия не больше указанного габарита и того же материала и цвета.
5. Материал и цвет, не указанные в данных изделия, приняты по концепции (лист 28): тон дерева — по полу, обивка — по вторичному цвету палитры; образцы согласовать до заказа.
6. Масса 1 ед. для изделий до 25 кг не указывается. Техника — по монтажным схемам изготовителя; выводы — по листам ЭОМ и ВК.

Допущения и предложения на листе. См. лист открытых вопросов (листы 8–10).

Изм.	Кол.уч	Лист	№ док.	Подп.	Дата
Разраб.		Кырлан А.С.			04.11.26
Пров.					
ГИП					
Н. контр.					
Утв.					

ГД-2026-010-АИ

Дом 331 м²

Общая площадь 270,67* м² · * размеры приняты, не замерены (реестр — л. 8–10, К-1)

Дизайн-проект интерьера

Стадия	Лист	Листов
РП	32	216

Спецификация мебели и оборудования

М б/м

Кырлан Александр Сергеевич

выпуск 04.11.2026 № 2a77323a49 · стр. 33 из 221

Спецификация мебели и оборудования (продолжение)

Форма 1 ГОСТ 21.110-2013 · позиции мебели — по плану расстановки

ПРЕДВАРИТЕЛЬНО · не для производства работ · открыто пунктов: 15 (реестр — л. 8–10)

Поз.	Наименование и техническая характеристика	Тип, марка, обозначение документа, опросного листа	Код продукции	Поставщик	Ед. измерения	Кол.	Масса 1 ед., кг	Примечание
Кб1	Письменный стол у окна, массив дуба на чёрном стальном подстолье; дерево — дуб массив, масло, металл — чёрный матовый; Ш×Г×В 1400×700×750 мм			аналог по характеристикам	шт.	1		пом. 2; замена ≤ габарита
Кб2	Кресло рабочее на колёсах, кожа коньячная; обивка кожа натуральная, коньяк; Ш×Г×В 600×600×900 мм			аналог по характеристикам	шт.	1		пом. 2; замена ≤ габарита
Кб3	Диван-кровать гостевой, шерстяной твид; обивка шерстяной твид, серо-оливковый меланж; Ш×Г×В 2000×900×850 мм			аналог по характеристикам	шт.	1		пом. 2; замена ≤ габарита
Кб4	Стеллаж для книг, чёрная сталь и полки из дуба; каркас — чёрная сталь, полки — массив дуба; Ш×Г×В 1600×400×2200 мм			аналог по характеристикам	шт.	1		пом. 2; крепление к стене; замена ≤ габарита
Гс1	ТВ-стена с камином, облицовка — колотый сланец; короб ГКЛ с облицовкой колотым сланцем, полка из массива дуба; Ш×Г×В 2400×450×600 мм			аналог по характеристикам	шт.	1		пом. 5; замена ≤ габарита
Гс2	Диван угловой, лён-рогожка; обивка лён-рогожка плотный, молочный; Ш×Г×В 3200×1000×820 мм			аналог по характеристикам	шт.	1		пом. 5; замена ≤ габарита
Гс3	Столик журнальный, столешница — сланец, подстолье дуб; столешница — сланец 20 мм, подстолье — массив дуба; Ш×Г×В 1200×700×420 мм			аналог по характеристикам	шт.	1		пом. 5; замена ≤ габарита
Гс4	Кресло, букле (овечья шерсть); обивка букле, овечья шерсть, молочный; Ш×Г×В 850×850×850 мм			аналог по характеристикам	шт.	1		пом. 5; замена ≤ габарита
Гс5	Кресло-качалка, кожа и ясень; обивка кожа натуральная, тёмный коньяк, дерево — ясень гнутый; Ш×Г×В 850×850×850 мм			аналог по характеристикам	шт.	1		пом. 5; замена ≤ габарита
Гс6	Буфет низкий, дуб; шпон, дуб натуральный, матовое масло; Ш×Г×В 1600×450×800 мм			аналог по характеристикам	шт.	1		пом. 5; крепление к стене; замена ≤ габарита
Пх2	Банкетка; Ш×Г×В 1000×400×450 мм			аналог по характеристикам	шт.	1		пом. 8; замена ≤ габарита
Гр2	Силовая стойка со скамьёй и штангой; стальная рама, порошковая окраска, чёрный матовый; под тренажёр — резиновый коврик 10 мм; Ш×Г×В 1200×1500×2300 мм			аналог по характеристикам	шт.	1		пом. 10; замена ≤ габарита
Гр3	Верстак с перфопанелью; шпон, дуб натуральный, матовое масло; Ш×Г×В 1800×700×900 мм			аналог по характеристикам	шт.	1		пом. 10; замена ≤ габарита
Гр4	Тренажёр гребной магнитный, складной; алюминиевая направляющая, маховик магнитный или водяной, сиденье на роликах; под тренажёр — резиновый коврик 10 мм; Ш×Г×В 2400×600×500 мм			аналог по характеристикам	шт.	1		пом. 10; замена ≤ габарита
Гр5	Стойка для гантелей 2 яруса, пары 4–20 кг; стальная рама, порошковая окраска, чёрный матовый; гантели с обрезиненными дисками; Ш×Г×В 1000×500×800 мм			аналог по характеристикам	шт.	1		пом. 10; крепление к стене; замена ≤ габарита
Гр6	Стенка шведская, бук, с навесным турником; массив бука, лак матовый; перекладины Ø40 шаг 200; крепление к стене — анкеры по основанию, не менее 6; Ш×Г×В 900×150×2300 мм			аналог по характеристикам	шт.	1		пом. 10; крепление к стене; замена ≤ габарита
Вр1	Стол летний; шпон, дуб натуральный, матовое масло; Ш×Г×В 1600×900×750 мм			аналог по характеристикам	шт.	1		пом. 11; замена ≤ габарита
Вр2	Диван плетёный; обивка — ткань, цвет Tikkurila V451; Ш×Г×В 2000×800×800 мм			аналог по характеристикам	шт.	1		пом. 11; замена ≤ габарита
Вр4, Вр5	Кресло плетёное; обивка — ткань, цвет Tikkurila V451; Ш×Г×В 800×800×800 мм			аналог по характеристикам	шт.	2		пом. 11; замена ≤ габарита
Вр6	Столик кофейный из тика; шпон, дуб натуральный, матовое масло; Ш×Г×В 1000×600×420 мм			аналог по характеристикам	шт.	1		пом. 11; замена ≤ габарита
Вр7	Стул обеденный к столу Вр1; обивка — ткань, цвет Tikkurila V451; каркас — дуб натуральный; Ш×Г×В 450×500×820 мм			аналог по характеристикам	шт.	6		пом. 11; замена ≤ габарита
М1	Кровать 1800×2000, изголовье — мягкое в шерстяном твиде; обивка шерстяной твид, серо-коричневый, дерево — дуб массив, царги и ножки; Ш×Г×В 1800×2100×450 мм			аналог по характеристикам	шт.	1		пом. 13; замена ≤ габарита
М2, М3	Тумба прикроватная, массив ореха; дерево — орех массив, масло; Ш×Г×В 500×400×550 мм			аналог по характеристикам	шт.	2		пом. 13; замена ≤ габарита
М4	Комод, дуб брашированный, фасады с кожаными ручками; дерево — дуб брашированный, масло; Ш×Г×В 1400×500×800 мм			аналог по характеристикам	шт.	1		пом. 13; крепление к стене; замена ≤ габарита
М5	Кресло для чтения, букле (овечья шерсть); обивка букле, овечья шерсть, молочный; Ш×Г×В 800×800×900 мм			аналог по характеристикам	шт.	1		пом. 13; замена ≤ габарита
Гм1	Ящики низкие под скатом (до колена 1200); шпон, дуб натуральный, матовое масло; Ш×Г×В 2600×500×1100 мм			аналог по характеристикам	шт.	1		пом. 14; замена ≤ габарита
С1	Кровать 1600×2000, изголовье — вертикальная рейка из ясеня; дерево — ясень массив, рейка; Ш×Г×В 1600×2100×450 мм			аналог по характеристикам	шт.	1		пом. 16; замена ≤ габарита

Допущения и предложения на листе

Основа листа: размеры и контуры этажей подобраны проектировщиком по составу помещений и площадям этажей с картинки 470 px (размеры на ней не читаются); обмер и исходный проект — задание (К-1); высоты: 1-й этаж 2800 мм, мансарда 2700 мм (горизонтальная часть) приняты; скаты кровли мансарды приняты по картинке: колено 1200 мм, уклон 45°, конёк вдоль длинной стороны; проект КР — задание (К-2); наружные стены 400 мм, перегородки 120 мм приняты (К-1); разрешённая мощность 15 кВт принята по типовым ТУ для частного дома (К-4); подрайон климата не задан — принят не северный (жилые от 2,5 м) (К-7).

См. лист открытых вопросов (лист 8, записи К-1, К-2, К-4, К-7).

Изм.	Кол.уч	Лист	№ док.	Подп.	Дата
Разраб.		Кырлан А.С.			04.11.26
Пров.					
ГИП					
Н. контр.					
Утв.					

ГД-2026-010-АИ

Дом 331 м²

Общая площадь 270,67* м² · * размеры приняты, не замерены (реестр — л. 8–10, К-1)

Дизайн-проект интерьера

Стадия	Лист	Листов
РП	33	216

Спецификация мебели и оборудования (продолжение)

М б/м

Кырлан Александр Сергеевич

Спецификация мебели и оборудования (продолжение)

Форма 1 ГОСТ 21.110-2013 · позиции мебели — по плану расстановки

ПРЕДВАРИТЕЛЬНО · не для производства работ · открыто пунктов: 15 (реестр — л. 8–10)

Поз.	Наименование и техническая характеристика	Тип, марка, обозначение документа, опросного листа	Код продукции	Поставщик	Ед. измерения	Кол.	Масса 1 ед., кг	Примечание
С2	Тумба подвесная, ясень; дерево — ясень шпон; Ш×Г×В 500×400×550 мм			аналог по характеристикам	шт.	1		пом. 16; крепление к стене; замена ≤ габарита
Сп1	Дорожка беговая складная, полотно 1400×500; стальная рама, порошковая окраска, чёрный матовый; под тренажёр резиновый коврик 10 мм; Ш×Г×В 2000×800×1400 мм			аналог по характеристикам	шт.	1		пом. 17; замена ≤ габарита
Сп2	Велотренажёр магнитный; стальная рама, порошковая окраска, чёрный матовый; под тренажёр — резиновый коврик 10 мм; Ш×Г×В 600×1100×1150 мм			аналог по характеристикам	шт.	1		пом. 17; замена ≤ габарита
Сп4	Стойка-этажерка для инвентаря: гантели 2–8 кг, эспандеры, ролик; стальная рама, порошковая окраска, чёрный матовый; гантели с обрезиненными дисками; Ш×Г×В 500×350×1000 мм			аналог по характеристикам	шт.	1		пом. 17; крепление к стене; замена ≤ габарита
Дт1	Кровать 900×2000 с бортиком, массив сосны; дерево — сосна массив, воск; Ш×Г×В 900×2000×450 мм			аналог по характеристикам	шт.	1		пом. 18; замена ≤ габарита
Дт2	Стол письменный, столешница ЛДСП светлый ясень, ножки — белая сталь; столешница ЛДСП «светлый ясень», ножки сталь, белая эмаль; Ш×Г×В 1200×600×750 мм			аналог по характеристикам	шт.	1		пом. 18; замена ≤ габарита
Дт4	Кровать 900×2000 с ящиками, массив берёзы; дерево — берёза массив, масло; Ш×Г×В 900×2000×450 мм			аналог по характеристикам	шт.	1		пом. 19; замена ≤ габарита
Дт5	Стол письменный растущий, берёзовая фанера на регулируемом каркасе; столешница — берёзовая фанера, лак; каркас сталь, тёмно-серая эмаль, регулировка 600–800; Ш×Г×В 1200×600×750 мм			аналог по характеристикам	шт.	1		пом. 19; замена ≤ габарита
	Техника встраиваемая и бытовая (покупные изделия), светильники под розетки							
	Посудомоечная машина встраиваемая, в модуле Кх2; ниша 600 мм	аналог по характеристикам: полновстраиваемая 60 см под фасад, ниша 600 × 862 мм, навеска фасада в комплекте		по выбору заказчика до изготовления мебели	шт.	1		пом. 1; по схеме изготовителя
	Варочная панель встраиваемая, индукционная, в модуле Кх3	аналог по характеристикам: индукционная 60 см, вырез 560 × 490 мм по шаблону модели		по выбору заказчика до изготовления мебели	шт.	1		пом. 1; по схеме изготовителя
	Духовой шкаф встраиваемый, в модуле Кх3	аналог по характеристикам: 60 см, лицевая панель 595 мм, ниша 560 × 600, глубина ≥ 550 мм, вентиляция за прибором		по выбору заказчика до изготовления мебели	шт.	1		пом. 1; по схеме изготовителя
	Холодильник встраиваемый, в модуле Кх5	аналог по характеристикам: полновстраиваемый под фасад, ниша 1780 × 560 × 550 мм, вентиляция решётка в цоколе, выход сверху		по выбору заказчика до изготовления мебели	шт.	1		пом. 1; по схеме изготовителя
	Вытяжка встраиваемая, над модулем Кх1 — предложено	аналог по характеристикам: производительность — по расчёту ОВ, шум ≤ 55 дБ(А)		по выбору заказчика до изготовления мебели	шт.	1		пом. 1; предложено, решает заказчик; вывод Р21** (ЭОМ)
	Стиральная машина — предложено	аналог по характеристикам: тип загрузки — по листу ВК, по листу ВК		по выбору заказчика до изготовления мебели	шт.	1		пом. 3; предложено, решает заказчик; вывод Р7** (ЭОМ)
	Стиральная машина — предложено	аналог по характеристикам: тип загрузки — по листу ВК, по листу ВК		по выбору заказчика до изготовления мебели	шт.	1		пом. 15; предложено, решает заказчик; вывод Р48** (ЭОМ)
	Стиральная машина, место по листу ВК (Сд4); Ш×Г 600×600 мм	аналог по характеристикам: тип загрузки — по листу ВК, в плане 600 × 600 мм (ширина × глубина), по листу ВК		по выбору заказчика до изготовления мебели	шт.	1		пом. 20; по схеме изготовителя
	Торшер, у поз. М4; абажур — ткань или опаловое стекло; лампа 2700 К			аналог по характеристикам	шт.	1		пом. 13; розетка Р46 (ЭОМ)
	Текстиль							
Т14	Рулонная штора кассетная, ткань димаут; полиэстер 100 %; цвет NCS S 2005-Y20R; карниз 890 мм, высота 2000 мм			аналог по характеристикам	шт.	1		пом. 1
Т7	Портьеры на люверсах, шерстяной твид; лён 100 %; цвет Farrow & Ball No. 40; карниз 1820 мм, высота 2790 мм, сборка 2			аналог по характеристикам	шт.	2		пом. 2
Т8	Тюль, льняная сетка; полиэстер 100 %; цвет NCS S 0804-Y30R; карниз 1820 мм, высота 2790 мм, сборка 2,5			аналог по характеристикам	шт.	1		пом. 2
Т9	Ковёр джутовый под диваном; шерсть 100 %; цвет Tikkurila X463; 1700×2300 мм			аналог по характеристикам	шт.	1		пом. 2; с подложкой

Допущения и предложения на листе

Основа листа: размеры и контуры этажей подобраны проектировщиком по составу помещений и площадям этажей с картинки 470 px (размеры на ней не читаются); обмер и исходный проект — задание (К-1); высоты: 1-й этаж 2800 мм, мансарда 2700 мм (горизонтальная часть) приняты; скаты кровли мансарды приняты по картинке: колено 1200 мм, уклон 45°, конёк вдоль длинной стороны; проект КР — задание (К-2); наружные стены 400 мм, перегородки 120 мм приняты (К-1); разрешённая мощность 15 кВт принята по типовым ТУ для частного дома (К-4); подрайон климата не задан — принят не северный (жилые от 2,5 м) (К-7).

Знак «**» — предложение проектировщика, заказчиком не утверждено (согласовать с заказчиком): Р21 — высота 2200 мм выше нормы 1 м (ПУЭ 6.6.30) по назначению: питание вытяжки над варочной панелью Кх3, розетка за съёмной панелью; Р7 — по образцу: Р7, Р8 и Р33 на высоте 1000 мм — верхний предел нормы (ПУЭ, п. 6.6.30, не выше 1 м); флаг решения снят; Р48 — по образцу: Р48, Р49 и Р33 на высоте 1000 мм — верхний предел нормы (ПУЭ, п. 6.6.30, не выше 1 м); флаг решения снят; сдвиг под раскладку плитки стены Б на 116 мм вдоль стены — ось на шве или в центре плитки, привязка по таблице листа.

См. лист открытых вопросов (лист 8, записи К-1, К-2, К-4, К-7).

Изм.	Кол.уч	Лист	№ док.	Подп.	Дата
Разраб.		Кырлан А.С.			04.11.26
Пров.					
ГИП					
Н. контр.					
Утв.					

ГД-2026-010-АИ

Дом 331 м²

Общая площадь 270,67* м² · * размеры приняты, не замерены (реестр — л. 8–10, К-1)

Дизайн-проект интерьера

Стадия	Лист	Листов
РП	34	216

Спецификация мебели и оборудования (продолжение)

М б/м

Кырлан Александр Сергеевич

выпуск 04.11.2026 № 2a7732a49 · стр. 35 из 221

Спецификация мебели и оборудования (продолжение)

Форма 1 ГОСТ 21.110-2013 · позиции мебели — по плану расстановки

ПРЕДВАРИТЕЛЬНО · не для производства работ · открыто пунктов: 15 (реестр — л. 8–10)

Поз.	Наименование и техническая характеристика	Тип, марка, обозначение документа, опросного листа	Код продукции	Поставщик	Ед. измерения	Кол.	Масса 1 ед., кг	Примечание
T10	Подушки на диван, кожа; букле (шерсть 60 %, полиэстер 40 %); цвет NCS S 3010-Y30R			аналог по характеристикам	шт.	3		пом. 2
T11	Подушки на кровать, акцент; хлопковый бархат 100 %; цвет Farrow & Ball No. 298			аналог по характеристикам	шт.	2		пом. 2
T12	Плед на кровать; шерсть мериноса 100 %; цвет Farrow & Ball No. 298			аналог по характеристикам	шт.	1		пом. 2
T1	Портьеры-волна, два полотна; лён 100 %; цвет NCS S 2005-Y20R; карниз 2150 мм, высота 2710 мм, сборка 2			аналог по характеристикам	шт.	2		пом. 5
T2	Тюль-вуаль, одно полотно; полиэстер 100 %; цвет NCS S 0804-Y30R; карниз 2150 мм, высота 2710 мм, сборка 2,5			аналог по характеристикам	шт.	1		пом. 5
T3	Ковёр мягкой группы, шерсть с джутом; шерсть 100 %; цвет Farrow & Ball No. 243; 3600×2400 мм			аналог по характеристикам	шт.	1		пом. 5; с подложкой
T4	Подушки декоративные на диван, лён; лён 100 %; цвет Farrow & Ball No. 226			аналог по характеристикам	шт.	3		пом. 5
T5	Подушки декоративные на диван, акцент; хлопковый бархат 100 %; цвет Farrow & Ball No. 93			аналог по характеристикам	шт.	2		пом. 5
T6	Плед на диван; шерсть мериноса 100 %; цвет Farrow & Ball No. 93			аналог по характеристикам	шт.	1		пом. 5
T40	Покрытие резиновое модульное 500×500×10 мм под спортзону; резиновая крошка SBR с цветными EPDM-вкраплениями, плиты 500×500, 10 мм; цвет Farrow & Ball No. 243; 1500×6300 мм			аналог по характеристикам	шт.	1		пом. 10
T13	Портьеры-волна, шерсть с блэкаут-подкладкой; лён 100 %; цвет Farrow & Ball No. 229; карниз 1800 мм, высота 2590 мм, сборка 2			аналог по характеристикам	шт.	2		пом. 13
T15	Тюль; полиэстер 100 %; цвет Little Greene No. 105; карниз 1800 мм, высота 2590 мм, сборка 2,5			аналог по характеристикам	шт.	1		пом. 13
T16	Ковёр под кроватью, шерсть ручного ткачества; шерсть 80 %, хлопок 20 %; цвет NCS S 2005-Y20R; 2800×1900 мм			аналог по характеристикам	шт.	1		пом. 13; с подложкой
T17	Подушки декоративные на кровать, шерсть-меланж; лён 100 %; цвет NCS S 2005-Y20R			аналог по характеристикам	шт.	3		пом. 13
T18	Подушки на кровать, акцент; хлопковый бархат 100 %; цвет NCS S 7020-G10Y			аналог по характеристикам	шт.	2		пом. 13
T19	Плед на кровать; шерсть мериноса 100 %; цвет NCS S 7020-G10Y			аналог по характеристикам	шт.	1		пом. 13
T20	Портьеры-волна, хлопок-сатин с блэкаут-подкладкой; лён 100 %; цвет Tikkurila X463; карниз 1820 мм, высота 2690 мм, сборка 2			аналог по характеристикам	шт.	2		пом. 16
T21	Тюль, лён-вуаль; полиэстер 100 %; цвет Little Greene No. 105; карниз 1820 мм, высота 2690 мм, сборка 2,5			аналог по характеристикам	шт.	1		пом. 16
T22	Ковёр под кроватью, шерсть с узором ромбы; шерсть 100 %; цвет NCS S 3010-Y30R; 2000×2500 мм			аналог по характеристикам	шт.	1		пом. 16; с подложкой
T23	Подушки декоративные на кровать, хлопок-рогожка; букле (шерсть 60 %, полиэстер 40 %); цвет Tikkurila X463			аналог по характеристикам	шт.	3		пом. 16
T24	Подушки на кровать, акцент; хлопковый бархат 100 %; цвет Farrow & Ball No. 64			аналог по характеристикам	шт.	2		пом. 16
T25	Плед на кровать; шерсть мериноса 100 %; цвет Farrow & Ball No. 64			аналог по характеристикам	шт.	1		пом. 16
T41	Коврик для йоги и растяжки 1830×610×6, TPE, нескользящий; TPE, 6 мм, двухслойный; цвет NCS S 3020-G30Y; 610×1830 мм			аналог по характеристикам	шт.	1		пом. 17
T26	Портьеры на люверсах, хлопок-канвас с блэкаут-подкладкой; лён 100 %; цвет Tikkurila V451; карниз 1820 мм, высота 2610 мм, сборка 2			аналог по характеристикам	шт.	2		пом. 18
T27	Тюль, хлопковая кисея; полиэстер 100 %; цвет NCS S 0804-Y30R; карниз 1820 мм, высота 2610 мм, сборка 2,5			аналог по характеристикам	шт.	1		пом. 18
T28	Ковёр под кроватью, хлопок, стираемый; шерсть 100 %; цвет NCS S 2005-Y20R; 1600×1200 мм			аналог по характеристикам	шт.	1		пом. 18; с подложкой
T29	Подушки на кровать, хлопок-вельвет; букле (шерсть 60 %, полиэстер 40 %); цвет Tikkurila V451			аналог по характеристикам	шт.	3		пом. 18
T30	Подушки на кровать, акцент; хлопковый бархат 100 %; цвет NCS S 3020-G30Y			аналог по характеристикам	шт.	2		пом. 18
T31	Плед на кровать; шерсть мериноса 100 %; цвет NCS S 3020-G30Y			аналог по характеристикам	шт.	1		пом. 18
T32	Портьеры-волна, лён-меланж с блэкаут-подкладкой; лён 100 %; цвет NCS S 2005-Y20R; карниз 1800 мм, высота 2590 мм, сборка 2			аналог по характеристикам	шт.	2		пом. 19
T33	Тюль, лён-вуаль в мелкую клетку; полиэстер 100 %; цвет Farrow & Ball No. 226; карниз 1800 мм, высота 2590 мм, сборка 2,5			аналог по характеристикам	шт.	1		пом. 19
T34	Ковёр под кроватью, шерсть с узором «горы»; шерсть 100 %; цвет NCS S 3010-Y30R; 1600×1200 мм			аналог по характеристикам	шт.	1		пом. 19; с подложкой

Допущения и предложения на листе

Основа листа: размеры и контуры этажей подобраны проектировщиком по составу помещений и площадям этажей с картинки 470 px (размеры на ней не читаются); обмер и исходный проект — задание (К-1); высоты: 1-й этаж 2800 мм, мансарда 2700 мм (горизонтальная часть) приняты; скаты кровли мансарды приняты по картинке: колено 1200 мм, уклон 45°, конёк вдоль длинной стороны; проект КР — задание (К-2); наружные стены 400 мм, перегородки 120 мм приняты (К-1); разрешённая мощность 15 кВт принята по типовым ТУ для частного дома (К-4); подрайон климата не задан — принят не северный (жилые от 2,5 м) (К-7).

См. лист открытых вопросов (лист 8, записи К-1, К-2, К-4, К-7).

Изм.	Кол.уч	Лист	№ док.	Подп.	Дата
Разраб.		Кырлан А.С.			04.11.26
Пров.					
ГИП					
Н. контр.					
Утв.					

ГД-2026-010-АИ

Дом 331 м²

Общая площадь 270,67* м² · * размеры приняты, не замерены (реестр — л. 8–10, К-1)

Дизайн-проект интерьера

Стадия	Лист	Листов
РП	35	216

Спецификация мебели и оборудования (продолжение)

М б/м

Кырлан Александр Сергеевич

Спецификация мебели и оборудования (продолжение)

Форма 1 ГОСТ 21.110-2013 · позиции мебели — по плану расстановки

ПРЕДВАРИТЕЛЬНО · не для производства работ · открыто пунктов: 15 (реестр — л. 8–10)

Поз.	Наименование и техническая характеристика	Тип, марка, обозначение документа, опросного листа	Код продукции	Поставщик	Ед. измерения	Кол.	Масса 1 ед., кг	Примечание
Т35	Подушки на кровать, хлопок-канвас с принтом; букле (шерсть 60 %, полиэстер 40 %); цвет Tikkurila X463			аналог по характеристикам	шт.	3		пом. 19
Т36	Подушки на кровать, акцент; хлопковый бархат 100 %; цвет NCS S 3040-Y70R			аналог по характеристикам	шт.	2		пом. 19
Т37	Плед на кровать; шерсть мериноса 100 %; цвет NCS S 3040-Y70R			аналог по характеристикам	шт.	1		пом. 19
	Декор							
ДК8	Часы настенные Ø400; 400×400 мм; центр на 1550 мм от пола			аналог по характеристикам	шт.	1	2	пом. 1; крепление: дюбель с крюком, 1 точка
ДК9	Хлорофитум хохлатый на подоконнике (отм. +0,800); 300×200 мм; низ на 800 мм от пола			аналог по характеристикам	шт.	1		пом. 1
ДК23	Ваза с тюльпанами на обеденном столе; 200×350 мм; на Кх8			аналог по характеристикам	шт.	1		пом. 1
ДК3	Картина над диваном: офорт в паспарту, рама — орех; 1000×700 мм; низ на 1100 мм от пола			аналог по характеристикам	шт.	1	4	пом. 2; крепление к стене
ДК28	Замиокулькас в кашпо Ø350; 350×350 мм			аналог по характеристикам	шт.	1		пом. 2
ДК1	Картина над буфетом: пейзаж, масло, рама — морёный дуб; 1200×900 мм; низ на 1000 мм от пола			аналог по характеристикам	шт.	1	6	пом. 5; крепление: планка на дюбелях, 4 точки
ДК2	Фикус лировидный в кашпо Ø400; 450×450 мм			аналог по характеристикам	шт.	1		пом. 5
ДК21	Оливковое дерево в кашпо Ø450; 450×450 мм			аналог по характеристикам	шт.	1		пом. 5
ДК22	Ваза с живыми цветами на журнальном столе; 200×350 мм; на Гс3			аналог по характеристикам	шт.	1		пом. 5
ДК5	Зеркало; рама — чёрный матовый; 800×1800 мм; низ на 550 мм от пола			аналог по характеристикам	шт.	1	18	пом. 8; крепление: анкер, 4 шт.
ДК31	Зеркало 1200×1500 для контроля техники, безопасное (плёнка), без рамы; 1200×1500 мм; низ на 600 мм от пола			аналог по характеристикам	шт.	1	22	пом. 10; крепление: анкер, 4 шт.
ДК24	Гортензия крупнолистная в кадке Ø500; 500×500 мм			аналог по характеристикам	шт.	1		пом. 11
ДК25	Самшит в кадке Ø450; 450×450 мм			аналог по характеристикам	шт.	1		пом. 11
ДК26	Папоротник нефролепис в ящике 600×250; 250×600 мм			аналог по характеристикам	шт.	1		пом. 11
ДК4	Картина над кроватью: акварель, рама — лиственница; 1000×700 мм; низ на 1300 мм от пола			аналог по характеристикам	шт.	1	4	пом. 13; крепление к стене
ДК27	Фикус каучуконосный в кашпо Ø400; 400×400 мм			аналог по характеристикам	шт.	1		пом. 13
ДК6	Картина над кроватью: натюрморт, масло, рама — тонкая латунь; 1000×700 мм; низ на 1300 мм от пола			аналог по характеристикам	шт.	1	4	пом. 16; крепление к стене
ДК7	Зеркало в рост в раме из ясеня; рама — чёрный матовый; 600×1600 мм; низ на 300 мм от пола			аналог по характеристикам	шт.	1	12	пом. 16; крепление: анкер для пустотелых оснований, 4 шт.
ДК30	Монстера в кашпо Ø450 с фитолампой; 450×450 мм			аналог по характеристикам	шт.	1		пом. 17
ДК10	Картина над кроватью: детская иллюстрация, рама — светлый ясень; 600×700 мм; низ на 1100 мм от пола			аналог по характеристикам	шт.	1	4	пом. 18; крепление к стене
ДК11	Зеркало безопасное (плёнка), рама — светлый ясень; рама — чёрный матовый; 500×1600 мм; низ на 300 мм от пола			аналог по характеристикам	шт.	1	12	пом. 18; крепление: анкер для пустотелых оснований, 4 шт.
ДК12	Картина над кроватью: детский принт, рама — белёный дуб; 600×700 мм; низ на 1100 мм от пола			аналог по характеристикам	шт.	1	4	пом. 19; крепление к стене
ДК13	Зеркало круглое Ø600 в кожаном ремне; рама — чёрный матовый; 600×600 мм; низ на 1150 мм от пола			аналог по характеристикам	шт.	1	12	пом. 19; крепление: анкер для пустотелых оснований, 4 шт.

Допущения и предложения на листе

Основа листа: размеры и контуры этажей подобраны проектировщиком по составу помещений и площадям этажей с картинки 470 px (размеры на ней не читаются); обмер и исходный проект — задание (К-1); высоты: 1-й этаж 2800 мм, мансарда 2700 мм (горизонтальная часть) приняты; скаты кровли мансарды приняты по картинке: колено 1200 мм, уклон 45°, конёк вдоль длинной стороны; проект КР — задание (К-2); наружные стены 400 мм, перегородки 120 мм приняты (К-1); разрешённая мощность 15 кВт принята по типовым ТУ для частного дома (К-4); подрайон климата не задан — принят не северный (жилые от 2,5 м) (К-7).

См. лист открытых вопросов (лист 8, записи К-1, К-2, К-4, К-7).

Изм.	Кол.уч	Лист	№ док.	Подп.	Дата
Разраб.		Кырлан А.С.			04.11.26
Пров.					
ГИП					
Н. контр.					
Утв.					

ГД-2026-010-АИ

Дом 331 м²

Общая площадь 270,67* м² · * размеры приняты, не замерены (реестр — л. 8–10, К-1)

Дизайн-проект интерьера	Стадия	Лист	Листов
	РП	36	216

Спецификация мебели и оборудования (продолжение)


М б/м

Кырлан Александр Сергеевич

План розеток и электровыводов · 1-й этаж

Розетки, выводы кабеля, щит · размеры в мм · высоты от чистого пола

ПРЕДВАРИТЕЛЬНО · не для производства работ · открыто пунктов: 15 (реестр — л. 8–10)

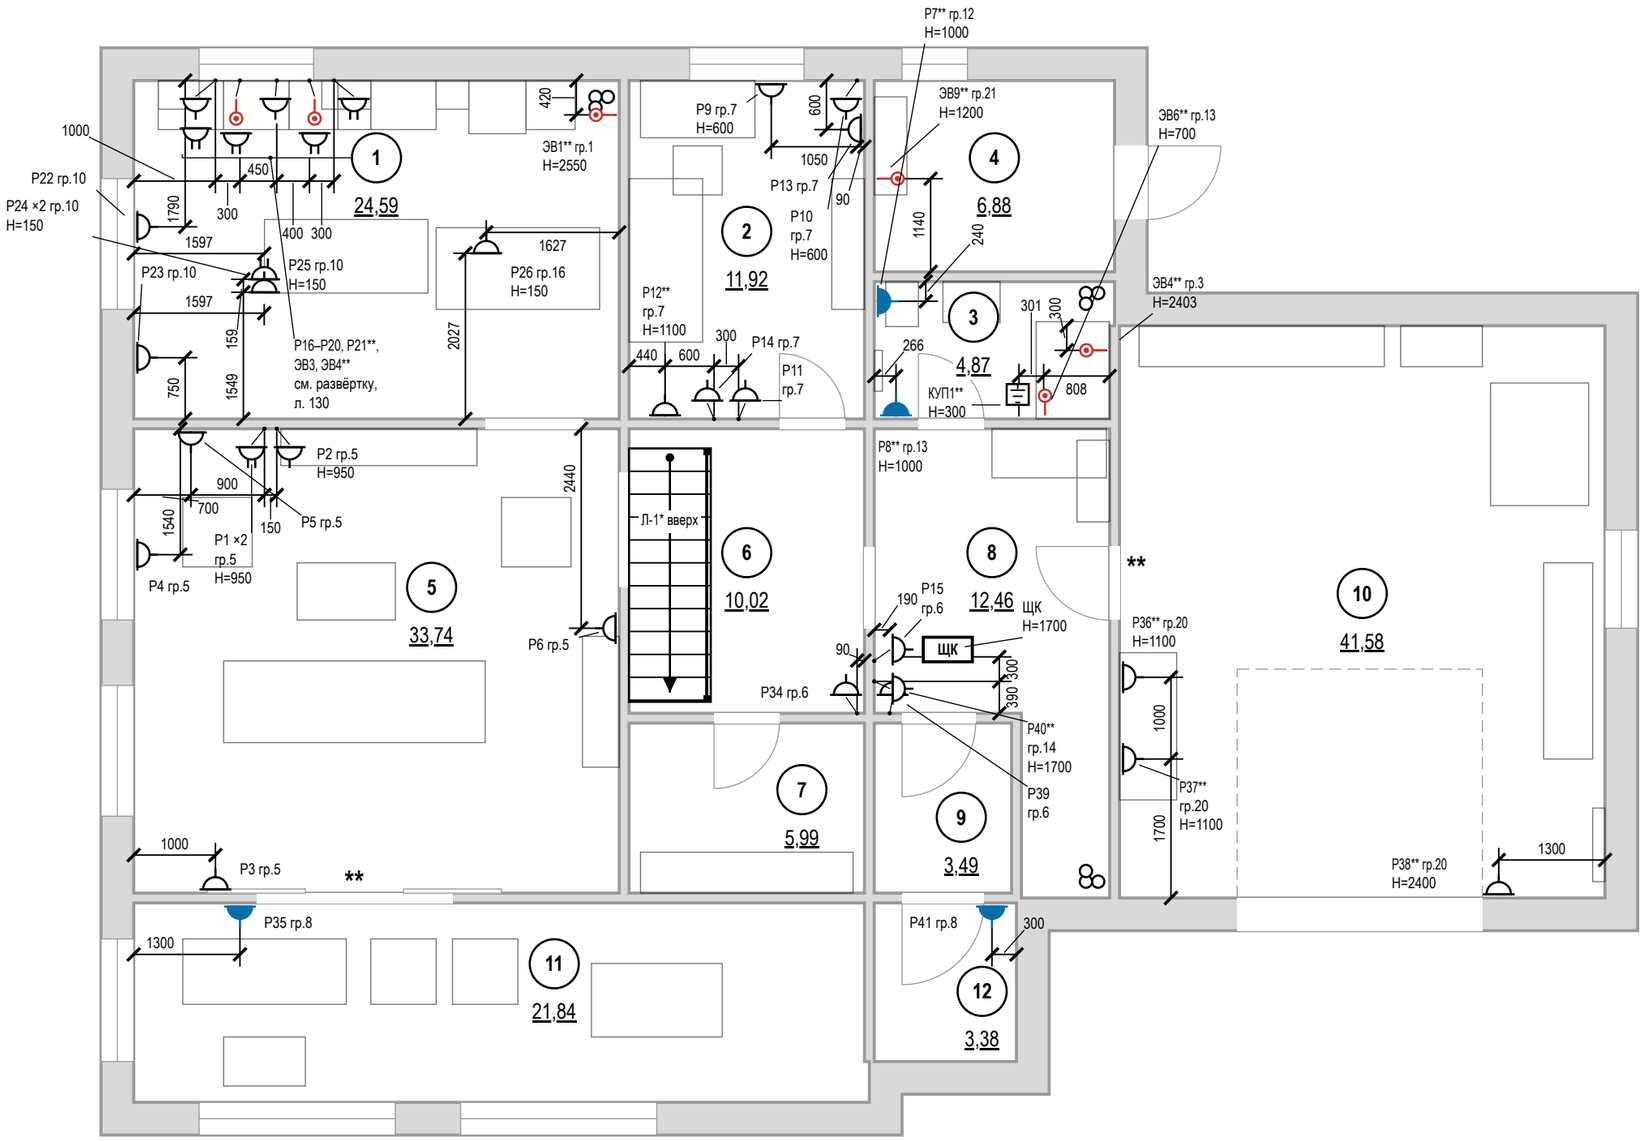

Условные обозначения

Знак	Тип изделия	Н, мм	Кол., шт
	Розетка с заземлением	300	12
	То же	у знака	12
	Блок розеток с заземлением, рамка 2 поста	у знака	6
	Розетка с заземлением IP44	300	2
	То же	у знака	2
	Вывод кабеля к прибору	у знака	6
КУП	КУП (уравнивание потенциалов)	300	1
ЩК	Щит квартирный	1700	1

розетка с заземляющим контактом; у знака — марка, ×N — постов в рамке, гр. — группа щита, Н — высота оси, мм

знак разведён для читаемости: точка на стене — у выноски, привязка — до неё

мебель и сантехприборы — подложка

стояк: К1 — канализация, В1 — ХВС, Т3 — ГВС

1 — номер помещения, площадь м²

Итого розеток (механизмов) — 40 шт; рамок — 34 шт: на 1 пост — 28, на 2 поста — 6.

Допущения и предложения на листе. Основа листа: размеры и контуры этажей подобраны проектировщиком по составу помещений и площадям этажей с картинки 470 px (размеры на ней не читаются); обмер и исходный проект — задание (К-1); высоты: 1-й этаж 2800 мм, мансарда 2700 мм (горизонтальная часть) приняты; скаты кровли мансарды приняты по картинке: колено 1200 мм, уклон 45°, конёк вдоль длинной стороны; проект КР — задание (К-2); наружные стены 400 мм, перегородки 120 мм приняты (К-1); разрешённая мощность 15 кВт принята по типовым ТУ для частного дома (К-4); подрайон климата не задан — принят не северный (жилые от 2,5 м) (К-7). Знак «*» — принято, не замерено (замерить): К-6: Л-1. Знак «**» — предложено, не утверждено (согласовать): Р21, Р12, Р7, Р8, ЭВ4, КУП1, ЭВ6, ЭВ9, Р40, Р36, Р37, Р38, ЭВ1. См. лист открытых вопросов (лист 8, записи К-1, К-2, К-4, К-6, К-7; лист 9, запись К-9).

Примечания

1. За отметку 0,000 принят уровень чистого пола. Высоты Н — от чистого пола до оси изделия; привязки — от чистовой грани стены до оси механизма (у рамки на несколько постов — до оси рамки).
2. Розетки без отметки Н у знака — на высоте 300 мм от чистого пола до оси механизма; выводы кабеля — по паспорту прибора.
3. Розетки в санузле — только вне зон 0–2 (ПУЭ 7.1.48, ГОСТ Р 50571.7.701-2024), IP44, через УЗО 30 мА.
4. Розеточные и мокрые линии — через УЗО или дифавтомат с током утечки не более 30 мА (ПУЭ 7.1.79); в санузле выполнить ДСУП (ПУЭ 7.1.87–7.1.88).
5. Кабель — медный, исполнение нг(A)-LS (ГОСТ 31565-2012); скрытая прокладка только горизонтально и вертикально, фактические трассы зафиксировать исполнительной схемой до закрытия отделкой.
6. Расчёт нагрузок, токов КЗ, селективности и сечений — по проекту ЭОМ организации с допуском СРО; лист задаёт состав, расположение и группы.
7. Выводы кухонной техники — после утверждения проекта кухни (ориентировочно); привязки выводов даны от осей модулей гарнитура и пересматриваются вместе с проектом кухни.
8. Электрический тёплый пол проектом не предусмотрен; при решении заказчика устроить — отдельный лист «План тёплых полов»: контуры с отступом 100 мм от стен и мебели без ножек, датчик в гофре, терморегулятор, своя группа щита через УЗО 30 мА.
9. Ведомости электроточек, изделий, светильников и расшифровка клавиш — лист 43.

1000 мм · печать 1:1

Изм.	Кол.уч	Лист	№ док.	Подп.	Дата
Разраб.		Кырлан А.С.			04.11.26
Пров.					
ГИП					
Н. контр.					
Утв.					

ГД-2026-010-АИ

Дом 331 м²

Общая площадь 270,67* м² · * размеры приняты, не замерены (реестр — л. 8–10, К-1)

Дизайн-проект интерьера

Стадия	Лист	Листов
РП	37	216

План розеток и электровыводов · 1-й этаж

М 1:75


Кырлан Александр Сергеевич

выпуск 04.11.2026 № 2a77323a49 · стр. 38 из 221

План розеток и электровыводов · Мансарда

Розетки, выводы кабеля, щит · размеры в мм · высоты от чистого пола

ПРЕДВАРИТЕЛЬНО · не для производства работ · открыто пунктов: 15 (реестр — л. 8–10)

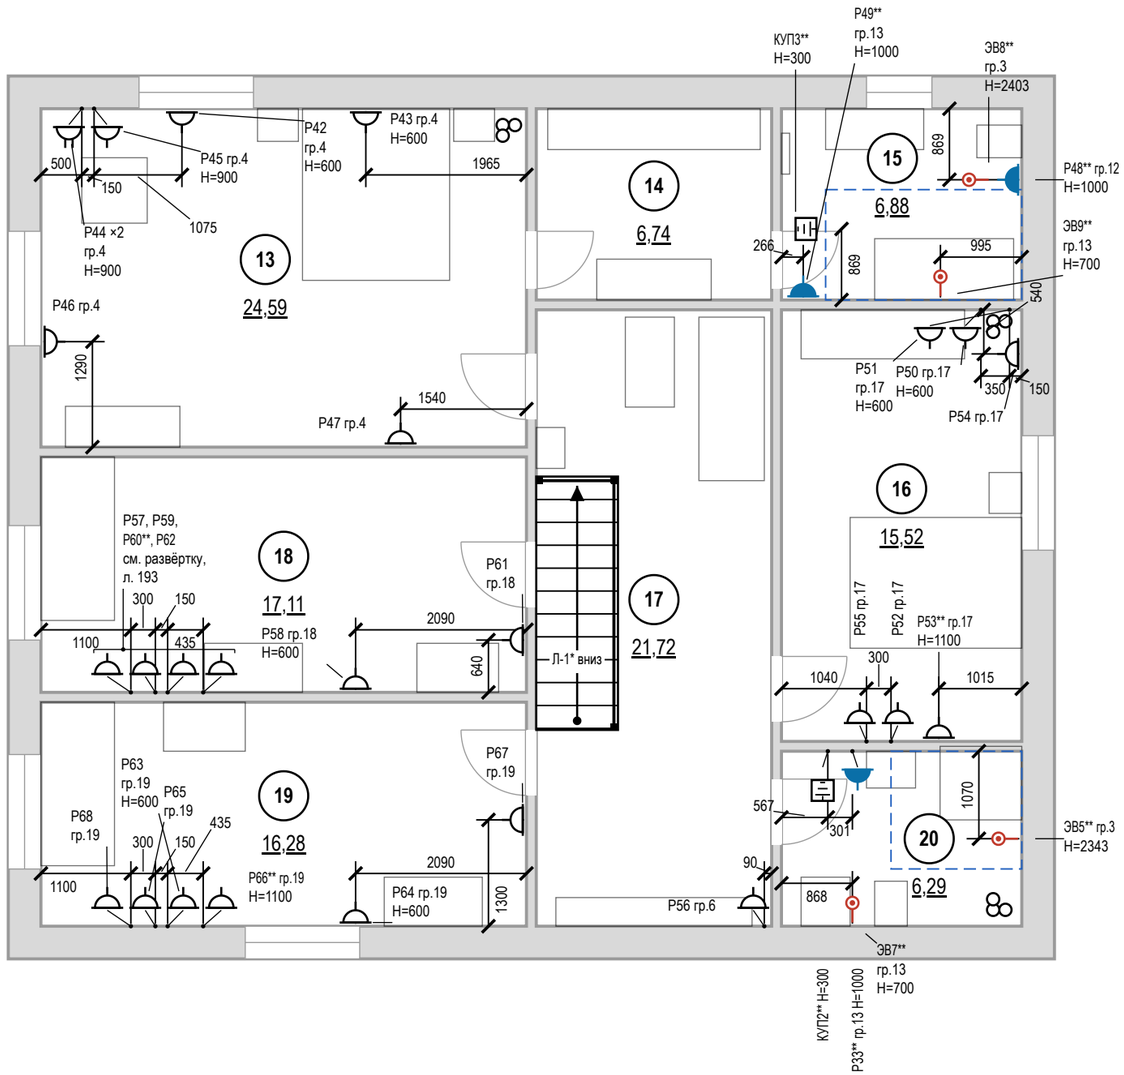

Условные обозначения

Знак	Тип изделия	Н, мм	Кол., шт
	Розетка с заземлением	300	12
	То же	у знака	12
	Блок розеток с заземлением, рамка 2 поста	900	1
	Розетка с заземлением IP44	1000	3
	Вывод кабеля к прибору	у знака	4
	КУП (уравнивание потенциалов)	300	2

розетка с заземляющим контактом; у знака — марка, ×N — постов в рамке, гр. — группа щита, Н — высота оси, мм

знак разведён для читаемости: точка на стене — у выноски, привязка — до неё

граница зоны 2 ванной (600 мм от ванны/поддона)

мебель и сантехприборы — подложка

стояк: К1 — канализация, В1 — ХВС, Т3 — ГВС

1 — номер помещения, площадь м²

Итого розеток (механизмов) — 29 шт; рамок — 28 шт: на 1 пост — 27, на 2 поста — 1.

Допущения и предложения на листе. Основа листа: размеры и контуры этажей подобраны проектировщиком по составу помещений и площадям этажей с картинки 470 px (размеры на ней не читаются); обмер и исходный проект — задание (К-1); высоты: 1-й этаж 2800 мм, мансарда 2700 мм (горизонтальная часть) приняты; скаты кровли мансарды приняты по картинке: колено 1200 мм, уклон 45°, конёк вдоль длинной стороны; проект КР — задание (К-2); наружные стены 400 мм, перегородки 120 мм приняты (К-1); разрешённая мощность 15 кВт принята по типовым ТУ для частного дома (К-4); подрайон климата не задан — принят не северный (жилые от 2,5 м) (К-7). Знак «*» — принято, не замерено (замерить): К-2: отметка чистого пола этажа «Мансарда» +3,150; К-6: Л-1. Знак «**» — предложено, не утверждено (согласовать): ЭВ9, Р48, Р49, ЭВ8, КУП3, Р53, Р60, Р66, Р33, КУП2, ЭВ7; ИЗ-1: ЭВ5. См. лист открытых вопросов (лист 8, записи К-1, К-2, К-4, К-6, К-7; лист 10, запись ИЗ-1).

Примечания

1. За отметку 0,000 принят уровень чистого пола. Высоты Н — от чистого пола до оси изделия; привязки — от чистовой грани стены до оси механизма (у рамки на несколько постов — до оси рамки).
2. Розетки без отметки Н у знака — на высоте 300 мм от чистого пола до оси механизма; выводы кабеля — по паспорту прибора.
3. Розетки в санузле — только вне зон 0–2 (ПУЭ 7.1.48, ГОСТ Р 50571.7.701-2024), IP44, через УЗО 30 мА.
4. Розеточные и мокрые линии — через УЗО или дифавтомат с током утечки не более 30 мА (ПУЭ 7.1.79); в санузле выполнить ДСУП (ПУЭ 7.1.87–7.1.88).
5. Кабель — медный, исполнение нг(А)-LS (ГОСТ 31565-2012); скрытая прокладка только горизонтально и вертикально, фактические трассы зафиксировать исполнительной схемой до закрытия отделкой.
6. Расчёт нагрузок, токов КЗ, селективности и сечений — по проекту ЭОМ организации с допуском СРО; лист задаёт состав, расположение и группы.
7. Электрический тёплый пол проектом не предусмотрен; при решении заказчика устроить — отдельный лист «План тёплых полов»: контуры с отступом 100 мм от стен и мебели без ножек, датчик в гофре, терморегулятор, своя группа щита через УЗО 30 мА.
8. Ведомости электроточек, изделий, светильников и расшифровка клавиш — лист 43.

1000 мм · печать 1:1

Изм.	Кол.уч	Лист	№ док.	Подп.	Дата
Разраб.		Кырлан А.С.			04.11.26
Пров.					
ГИП					
Н. контр.					
Утв.					

ГД-2026-010-АИ

Дом 331 м²

Общая площадь 270,67* м² · * размеры приняты, не замерены (реестр — л. 8–10, К-1)

Дизайн-проект интерьера

Стадия	Лист	Листов
РП	38	216

План розеток и электровыводов · Мансарда

М 1:75


Кырлан Александр Сергеевич

выпуск 04.11.2026 № 2a77323a49 · стр. 39 из 221

План освещения · 1-й этаж

Светильники, группы включения, извещатели · размеры в мм

ПРЕДВАРИТЕЛЬНО · не для производства работ · открыто пунктов: 15 (реестр — л. 8–10)

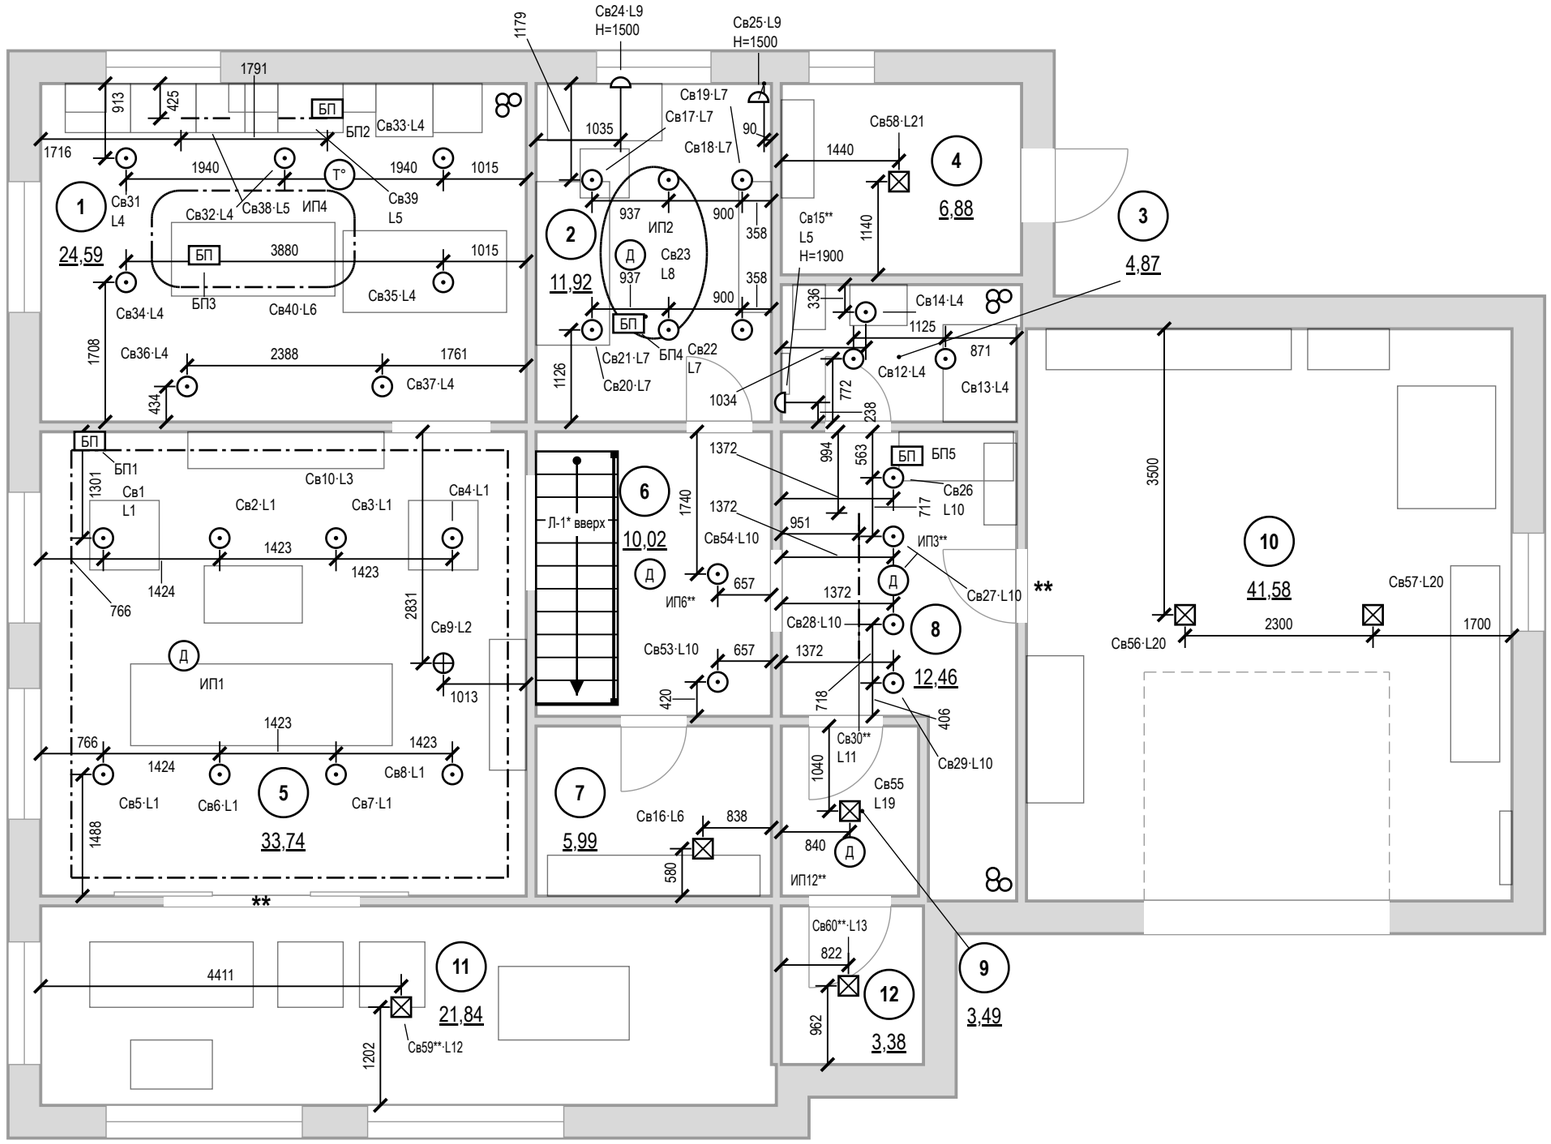

Условные обозначения

- светильник встраиваемый точечный
- светильник потолочный накладной
- светильник подвесной
- светильник настенный (бра), H — высота оси
- светодиодная лента в профиле / в карнизе короба
- Св1·L1 — марка светильника (как в ведомости и на развёртках) · группа включения L (лист 41)
- Д — извещатель пожарный дымовой автономный
- Т° — извещатель пожарный тепловой
- БП — блок питания LED, с доступом (люк от 100×100 мм)
- мебель и сантехприборы — подложка
- стояк: К1 — канализация, В1 — ХВС, Т3 — ГВС
- 1 — номер помещения, площадь м²

Допущения и предложения на листе

Основа листа: размеры и контуры этажей подобраны проектировщиком по составу помещений и площадям этажей с картинки 470 px (размеры на ней не читаются); обмер и исходный проект — задание (К-1); высоты: 1-й этаж 2800 мм, мансарда 2700 мм (горизонтальная часть) приняты; скаты кровли мансарды приняты по картинке: колено 1200 мм, уклон 45°, конёк вдоль длинной стороны; проект КР — задание (К-2); наружные стены 400 мм, перегородки 120 мм приняты (К-1); разрешённая мощность 15 кВт принята по типовым ТУ для частного дома (К-4); подрайон климата не задан — принят не северный (жилые от 2,5 м) (К-7).

Знак «*» — принято, не замерено и не подтверждено (замерить на объекте): К-6: Л-1 — габарит марша снят с картинки заказчика (11 проступей в холле 3,6 м), а до отм. +3,150 нужно 18 подъёмов — одномаршевая не встаёт: решение по К-6.

Знак «**» — предложение проектировщика, заказчиком не утверждено (согласовать с заказчиком): Св15 — Сдвиг под раскладку плитки стены Г на 52 мм вдоль стены — ось на шве или в центре плитки, привязка по таблице листа; ИП6, ИП3 — дымовой автономный вместо теплового образца: жилой дом — автономные дымовые в путях эвакуации (СП 486, пункт сверить по действующей редакции); Св30 — открытая лента в накладном профиле вместо «в коробе»: короба в потолке нет — подвесной потолок помещения без короба и ниши LED; ИП12 — жилой дом — автономные дымовые извещатели в жилых комнатах и путях эвакуации (СП 486, пункт сверить по действующей редакции); место — центр помещения, не ближе 500 мм к светильнику; дверь пом. 8 (стена Б) — дверь гаража в дом — СП 55.13330.2016 п. 7.7: EI 30, уплотнение в притворах, самозакрывание (доводчик); ИЗ-1: Св59, Св60 — накладной вместо встраиваемого: потолок окрашенный, без подвесной конструкции (летнее помещение) — корпусу встраиваемого негде стоять; К-9: дверь пом. 5 (стена В) — проём 2400×2100 на веранду с картинки: одной распашной створкой не закрывается (полотна 600–900) — раздвижная двустворчатая, остеклённая; система и полотна — по каталогу после утверждения автором.

Изменения по листу без подписи: ИЗ-1.

См. лист открытых вопросов (лист 8, записи К-1, К-2, К-4, К-6, К-7; лист 9, запись К-9; лист 10, запись ИЗ-1).

Примечания

1. За отметку 0,000 принят уровень чистого пола. Высоты H — от чистого пола до оси изделия; привязки — от чистовой грани стены до оси механизма (у рамки на несколько постов — до оси рамки).
2. Высота установки, не указанная на плане: светильники — на потолке; настенные — по отметке H у знака. Привязки — до оси светильника от чистовой грани стены, по рядам.
3. Во влажных помещениях — светильники не ниже IP44; в зонах 0–2 ванной — по ГОСТ Р 50571.7.701-2024 (зона 1 — IPX5).
4. LED-лента в карнизе подсветки короба — по линии карниза с плана потолков; блок питания — в люке короба (БП на плане), питание ленты длиннее 5 м — с двух концов.
5. Розеточные и мокрые линии — через УЗО или дифавтомат с током утечки не более 30 мА (ПУЭ 7.1.79); в санузле выполнить ДСУП (ПУЭ 7.1.87–7.1.88).
6. Кабель — медный, исполнение нг(А)-LS (ГОСТ 31565-2012); скрытая прокладка только горизонтально и вертикально, фактические трассы зафиксировать исполнительной схемой до закрытия отделкой.
7. Расчёт нагрузок, токов КЗ, селективности и сечений — по проекту ЭОМ организации с допуском СРО; лист задаёт состав, расположение и группы.
8. Ведомость светильников (тип, количество, мощность, поток, Tц, Ra) — лист 71.
9. Оценка освещённости (по норме СанПиН 1.2.3685-21, табл. 5.52, на полу; не светотехнический расчёт, декоративная подсветка в оценку не входит) — лист 43.

1000 мм · печать 1:1

Изм.	Кол.уч	Лист	№ док.	Подп.	Дата
Разраб.		Кырлан А.С.			04.11.26
Пров.					
ГИП					
Н. контр.					
Утв.					

ГД-2026-010-АИ

Дом 331 м²

Общая площадь 270,67* м² · * размеры приняты, не замерены (реестр — л. 8–10, К-1)

Дизайн-проект интерьера

Стадия	Лист	Листов
РП	39	216

План освещения · 1-й этаж


М 1:75

Кырлан Александр Сергеевич

выпуск 04.11.2026 № 2a77323a49 · стр. 40 из 221

План освещения · Мансарда

Светильники, группы включения, извещатели · размеры в мм

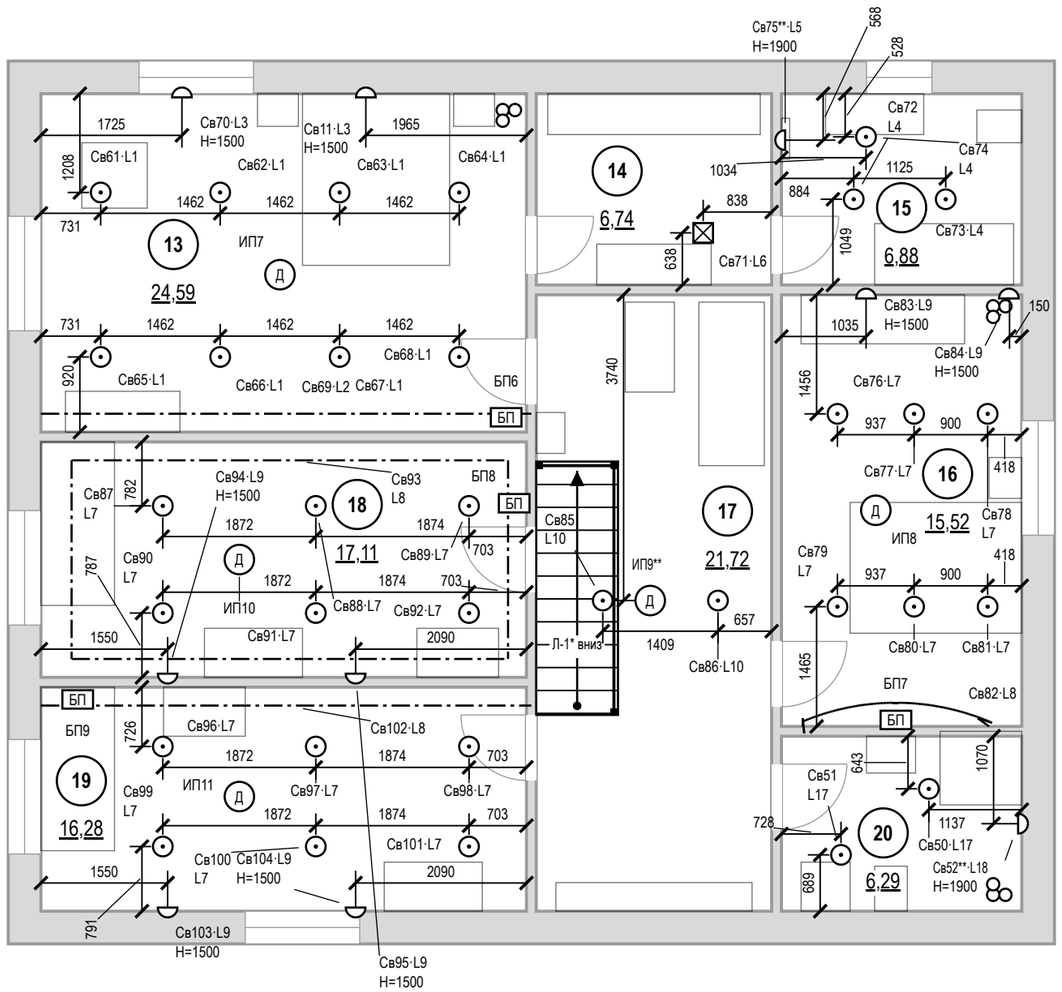

Условные обозначения

- светильник встраиваемый точечный
- светильник потолочный накладной
- светильник настенный (бра), H — высота оси
- светодиодная лента в профиле / в карнизе короба
- Св1·L1 — марка светильника (как в ведомости и на развёртках) · группа включения L (лист 41)
- Д — извещатель пожарный дымовой автономный
- БП — блок питания LED, с доступом (люк от 100×100 мм)
- мебель и сантехприборы — подложка
- стояк: К1 — канализация, В1 — ХВС, Т3 — ГВС
- 1 — номер помещения, площадь м²

Допущения и предложения на листе

Основа листа: размеры и контуры этажей подобраны проектировщиком по составу помещений и площадям этажей с картинки 470 px (размеры на ней не читаются); обмер и исходный проект — задание (К-1); высоты: 1-й этаж 2800 мм, мансарда 2700 мм (горизонтальная часть) приняты; скаты кровли мансарды приняты по картинке: колено 1200 мм, уклон 45°, конёк вдоль длинной стороны; проект КР — задание (К-2); наружные стены 400 мм, перегородки 120 мм приняты (К-1); разрешённая мощность 15 кВт принята по типовым ТУ для частного дома (К-4); подрайон климата не задан — принят не северный (жилые от 2,5 м) (К-7).

Знак «*» — принято, не замерено и не подтверждено (замерить на объекте): К-2: отметка чистого пола этажа «Мансарда» +3,150 — принята без источника, все отметки мансарды считаются от неё; К-6: Л-1 — габарит марша снят с картинки заказчика (11 проступей в холле 3,6 м), а до отм. +3,150 нужно 18 подъёмов — одномаршевая не встаёт: решение по К-6.

Знак «**» — предложение проектировщика, заказчиком не утверждено (согласовать с заказчиком): Св75 — Сдвиг под раскладку плитки стены Г на 32 мм вдоль стены — ось на шве или в центре плитки, привязка по таблице листа; ИП9 — дымовой автономный вместо теплового образца: жилой дом — автономные дымовые в путях эвакуации (СП 486, пункт сверить по действующей редакции); ИЗ-1: Св52 — Сдвиг под раскладку плитки стены Б на 25 мм вдоль стены — ось на шве или в центре плитки, привязка по таблице листа.

Изменения по листу без подписи: ИЗ-1.

См. лист открытых вопросов (лист 8, записи К-1, К-2, К-4, К-6, К-7; лист 10, запись ИЗ-1).

Примечания

1. За отметку 0,000 принят уровень чистого пола. Высоты H — от чистого пола до оси изделия; привязки — от чистовой грани стены до оси механизма (у рамки на несколько постов — до оси рамки).
2. Высота установки, не указанная на плане: светильники — на потолке; настенные — по отметке H у знака. Привязки — до оси светильника от чистовой грани стены, по рядам.
3. Во влажных помещениях — светильники не ниже IP44; в зонах 0–2 ванной — по ГОСТ Р 50571.7.701-2024 (зона 1 — IPX5).
4. LED-лента в карнизе подсветки короба — по линии карниза с плана потолков; блок питания — в люке короба (БП на плане), питание ленты длиннее 5 м — с двух концов.
5. Розеточные и мокрые линии — через УЗО или дифавтомат с током утечки не более 30 мА (ПУЭ 7.1.79); в санузле выполнить ДСУП (ПУЭ 7.1.87–7.1.88).
6. Кабель — медный, исполнение нг(A)-LS (ГОСТ 31565-2012); скрытая прокладка только горизонтально и вертикально, фактические трассы зафиксировать исполнительной схемой до закрытия отделкой.
7. Расчёт нагрузок, токов КЗ, селективности и сечений — по проекту ЭОМ организации с допуском СРО; лист задаёт состав, расположение и группы.
8. Ведомость светильников (тип, количество, мощность, поток, Tц, Ra) — лист 71.
9. Оценка освещённости (по норме СанПиН 1.2.3685-21, табл. 5.52, на полу; не светотехнический расчёт, декоративная подсветка в оценку не входит) — лист 43.

1000 мм · печать 1:1

Изм.	Кол.уч	Лист	№ док.	Подп.	Дата
Разраб.		Кырлан А.С.			04.11.26
Пров.					
ГИП					
Н. контр.					
Утв.					

ГД-2026-010-АИ

Дом 331 м²

Общая площадь 270,67* м² · * размеры приняты, не замерены (реестр — л. 8–10, К-1)

Дизайн-проект интерьера

Стадия	Лист	Листов
РП	40	216

План освещения · Мансарда

М 1:75


Кырлан Александр Сергеевич

выпуск 04.11.2026 № 2a77323a49 · стр. 41 из 221

План выключателей и схема включения · 1-й этаж

Выключатели S, группы включения L, линии связи · размеры в мм

ПРЕДВАРИТЕЛЬНО · не для производства работ · открыто пунктов: 15 (реестр — л. 8–10)

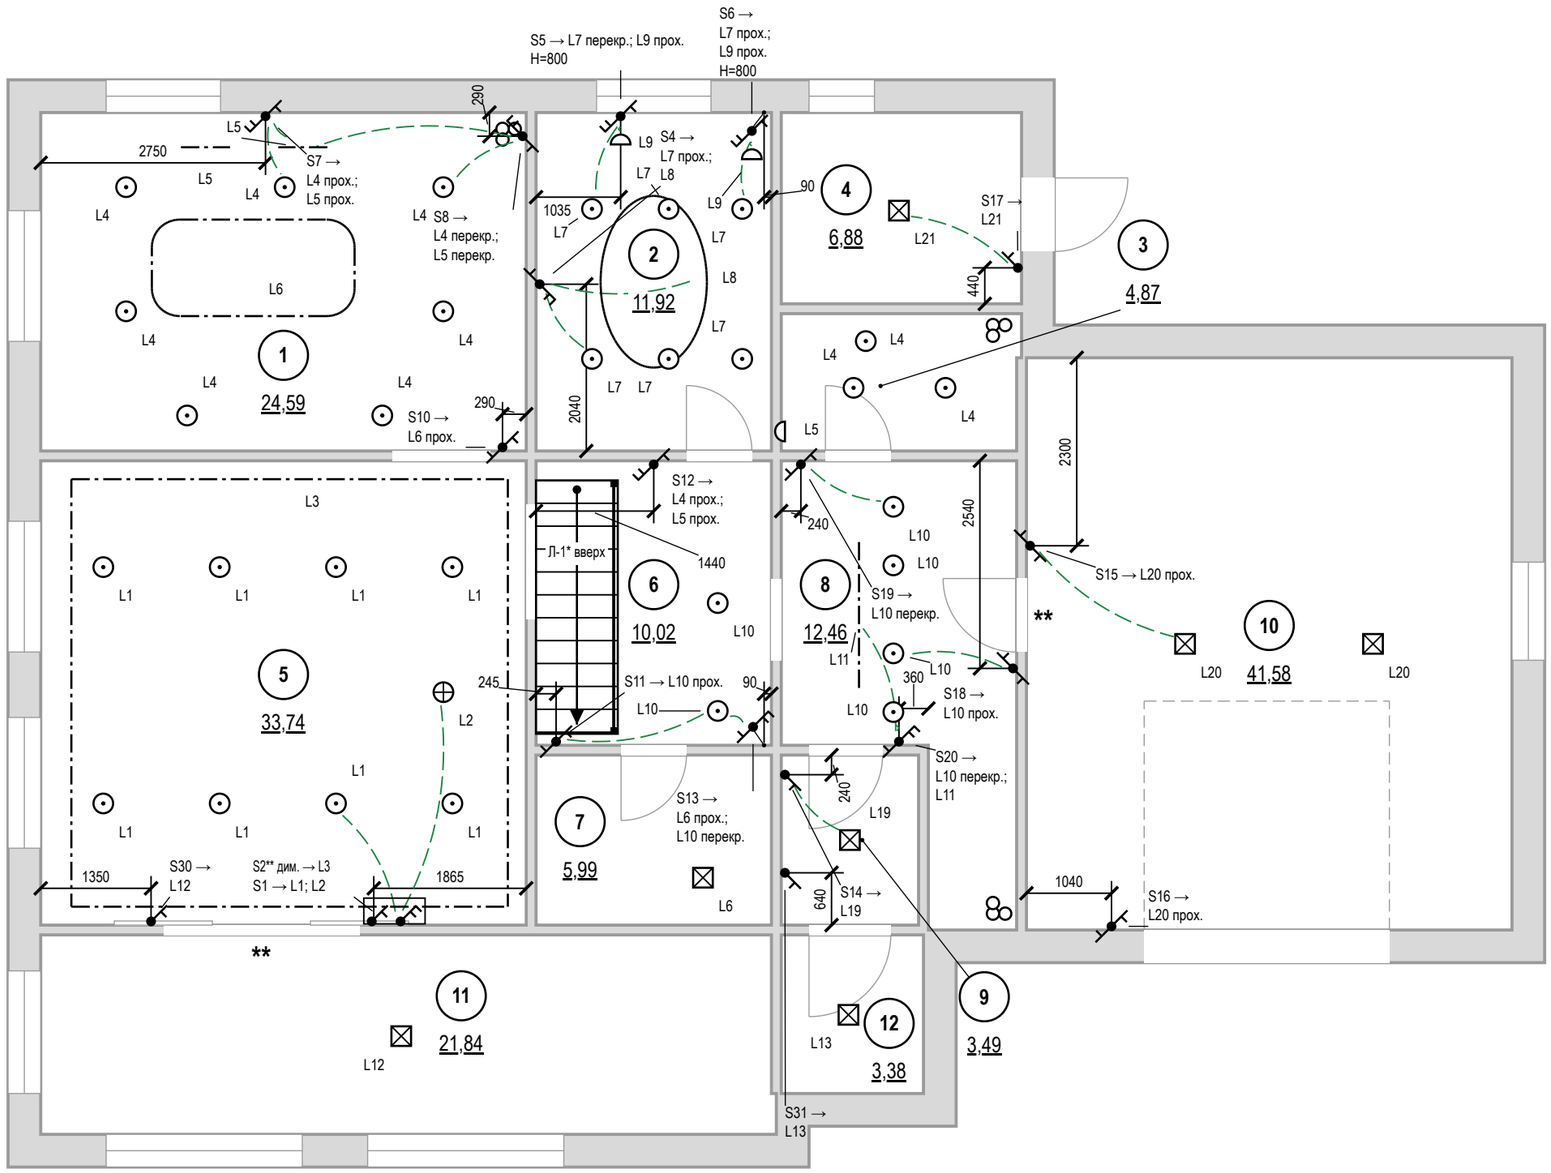

Условные обозначения

- выключатель одноклавишный
- выключатель двухклавишный (флажков — по числу клавиш)
- выключатель с проходной или перекрёстной клавишей (обратный флажок); тип клавиши — в подписи
- S1 → — марка → группы по клавишам (через «;»): прох. — проходной, перекр. — перекрёстный, дим. — светорегулятор; H — высота
- связь: выключатель → ближайший светильник группы в том же помещении (не трасса кабеля); полный состав группы — по номеру L
- светильник встраиваемый точечный
- светильник потолочный накладной
- светильник подвесной
- светильник настенный (бра), H — высота оси
- светодиодная лента в профиле / в карнизе короба
- L1 — группа включения у светильника
- стояк: К1 — канализация, В1 — ХВС, Т3 — ГВС
- 1 — номер помещения, площадь м²

Допущения и предложения на листе

Основа листа: размеры и контуры этажей подобраны проектировщиком по составу помещений и площадям этажей с картинки 470 px (размеры на ней не читаются); обмер и исходный проект — задание (К-1); высоты: 1-й этаж 2800 мм, мансарда 2700 мм (горизонтальная часть) приняты; скаты кровли мансарды приняты по картинке: колено 1200 мм, уклон 45°, конёк вдоль длинной стороны; проект КР — задание (К-2); наружные стены 400 мм, перегородки 120 мм приняты (К-1); разрешённая мощность 15 кВт принята по типовым ТУ для частного дома (К-4); подрайон климата не задан — принят не северный (жилые от 2,5 м) (К-7).

Знак «*» — принято, не замерено и не подтверждено (замерить на объекте): К-6: Л-1 — габарит марша снят с картинки заказчика (11 проступей в холле 3,6 м), а до отм. +3,150 нужно 18 подъёмов — одномаршевая не встаёт: решение по К-6.

Знак «**» — предложение проектировщика, заказчиком не утверждено (согласовать с заказчиком): S2 — светорегулятор добавлен под диммируемую ленту L3; уровни сценариев выбраны конвейером; дверь пом. 8 (стена Б) — дверь гаража в дом — СП 55.13330.2016 п. 7.7: EI 30, уплотнение в притворах, самозакрывание (доводчик); К-9: дверь пом. 5 (стена В) — проём 2400×2100 на веранду с картинки: одной распашной створкой не закрывается (полотна 600–900) — раздвижная двустворчатая, остеклённая; система и полотна — по каталогу после утверждения автором.

Изменения по листу без подписи: ИЗ-1.

См. лист открытых вопросов (лист 8, записи К-1, К-2, К-4, К-6, К-7; лист 9, запись К-9; лист 10, запись ИЗ-1).

Примечания

1. За отметку 0,000 принят уровень чистого пола. Высоты H — от чистого пола до оси изделия; привязки — от чистовой грани стены до оси механизма (у рамки на несколько постов — до оси рамки).
2. Высота установки, не указанная на плане: выключатели — 900 мм от чистого пола (у кровати и другие — H у марки), со стороны дверной ручки (ПУЭ 7.1.51).
3. Какой выключатель какие светильники включает — по номеру группы L: у выключателя (S1 → L1; L2 — клавиши по порядку) и у каждого светильника. Пунктир подсказка к ближайшему светильнику группы в том же помещении (не дальше 3 м), это не трасса кабеля; выключатель за стеной (у двери санузла) и далёкая группа — только номер группы.
4. Группы из нескольких мест (L4 — S7, S8, S12; L5 — S7, S8, S12; L6 — S10, S13; L7 — S4, S5, S6; L9 — S5, S6; L10 — S11, S13, S18, S19, S20; L20 — S15, S16): на крайних местах — проходные клавиши, на промежуточных — перекрёстные; механизмы — в ведомости изделий.
5. Светорегулятор — по заднему фронту (для LED-драйверов), совместимость с драйверами проверить до закупки.
6. Вентиляторы санузлов (выводы ЭВ на плане розеток) включаются вместе с основным светом помещения, отключаются с задержкой — таймер выбега в вентиляторе.
7. Розеточные и мокрые линии — через УЗО или дифавтомат с током утечки не более 30 мА (ПУЭ 7.1.79); в санузле выполнить ДСУП (ПУЭ 7.1.87–7.1.88).
8. Кабель — медный, исполнение нг(А)-LS (ГОСТ 31565-2012); скрытая прокладка только горизонтально и вертикально, фактические трассы зафиксировать исполнительной схемой до закрытия отделкой.
9. Расчёт нагрузок, токов КЗ, селективности и сечений — по проекту ЭОМ организации с допуском СРО; лист задаёт состав, расположение и группы.
10. Расшифровка клавиш и ведомость изделий — лист 43.

1000 мм · печать 1:1

Изм.	Кол.уч	Лист	№ док.	Подп.	Дата
Разраб.		Кырлан А.С.			04.11.26
Пров.					
ГИП					
Н. контр.					
Утв.					

ГД-2026-010-АИ

Дом 331 м²

Общая площадь 270,67* м² · * размеры приняты, не замерены (реестр — л. 8–10, К-1)


Дизайн-проект интерьера	Стадия	Лист	Листов
	РП	41	216
План выключателей и схема включения · 1-й этаж М 1:75	**Кырлан Александр Сергеевич**		

выпуск 04.11.2026 № 2a77323a49 · стр. 42 из 221

План выключателей и схема включения · Мансарда

Выключатели S, группы включения L, линии связи · размеры в мм

ПРЕДВАРИТЕЛЬНО · не для производства работ · открыто пунктов: 15 (реестр — л. 8–10)

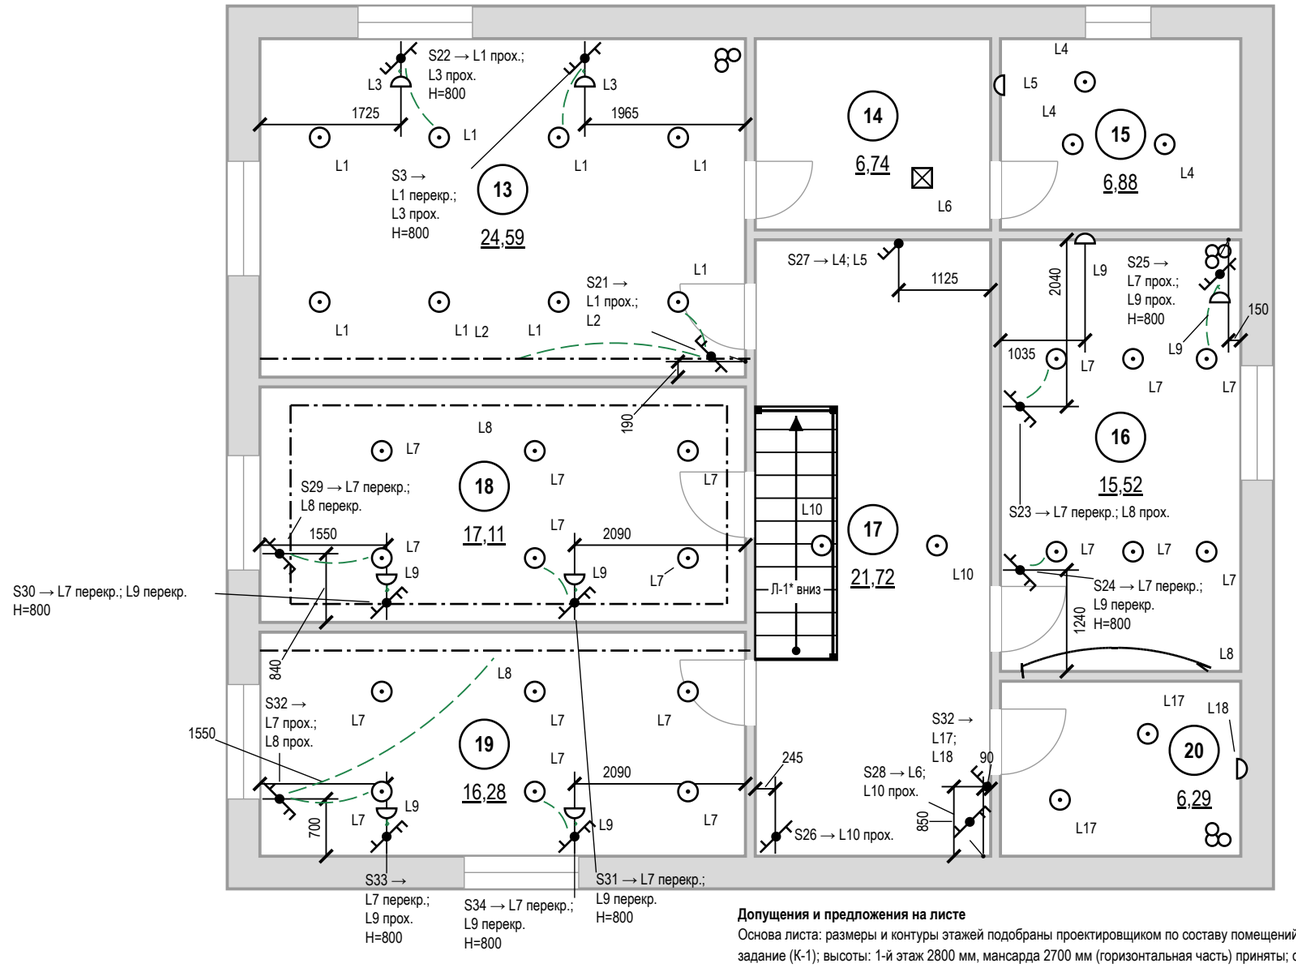

Условные обозначения

- выключатель двухклавишный (флажков — по числу клавиш)
- выключатель с проходной или перекрёстной клавишей (обратный флажок); тип клавиши — в подписи
- S1 → — марка → группы по клавишам (через «;»): прох. — проходной, перекр. — перекрёстный, дим. — светорегулятор; Н — высота
- связь: выключатель → ближайший светильник группы в том же помещении (не трасса кабеля); полный состав группы — по номеру L
- светильник встраиваемый точечный
- светильник потолочный накладной
- светильник настенный (бра), Н — высота оси
- светодиодная лента в профиле / в карнизе короба
- L1 — группа включения у светильника
- стояк: К1 — канализация, В1 — ХВС, Т3 — ГВС
- 1 — номер помещения, площадь м²

Допущения и предложения на листе

Основа листа: размеры и контуры этажей подобраны проектировщиком по составу помещений и площадям этажей с картинки 470 px (размеры на ней не читаются); обмер и исходный проект — задание (К-1); высоты: 1-й этаж 2800 мм, мансарда 2700 мм (горизонтальная часть) приняты; скаты кровли мансарды приняты по картинке: колено 1200 мм, уклон 45°, конёк вдоль длинной стороны; проект КР — задание (К-2); наружные стены 400 мм, перегородки 120 мм приняты (К-1); разрешённая мощность 15 кВт принята по типовым ТУ для частного дома (К-4); подрайон климата не задан — принят не северный (жилые от 2,5 м) (К-7).

Знак «*» — принято, не замерено и не подтверждено (замерить на объекте): К-2: отметка чистого пола этажа «Мансарда» +3,150 — принята без источника, все отметки мансарды считаются от неё; К-6: Л-1 — габарит марша снят с картинки заказчика (11 проступей в холле 3,6 м), а до отм. +3,150 нужно 18 подъёмов — одномаршевая не встаёт: решение по К-6.

Изменения по листу без подписи: ИЗ-1.

См. лист открытых вопросов (лист 8, записи К-1, К-2, К-4, К-6, К-7; лист 10, запись ИЗ-1).

Примечания

1. За отметку 0,000 принят уровень чистого пола. Высоты Н — от чистого пола до оси изделия; привязки — от чистовой грани стены до оси механизма (у рамки на несколько постов — до оси рамки).
2. Высота установки, не указанная на плане: выключатели — 900 мм от чистого пола (у кровати и другие — Н у марки), со стороны дверной ручки (ПУЭ 7.1.51).
3. Какой выключатель какие светильники включает — по номеру группы L: у выключателя (S1 → L1; L2 — клавиши по порядку) и у каждого светильника. Пунктир подсказка к ближайшему светильнику группы в том же помещении (не дальше 3 м), это не трасса кабеля; выключатель за стеной (у двери санузла) и далёкая группа — только номер группы.
4. Группы из нескольких мест (L1 — S3, S21, S22; L3 — S3, S22; L7 — S23, S24, S25, S29, S30, S31, S32, S33, S34; L8 — S23, S29, S32; L9 — S24, S25, S30, S31, S33, S34; L10 — S26, S28): на крайних местах — проходные клавиши, на промежуточных — перекрёстные; механизмы — в ведомости изделий.
5. Розеточные и мокрые линии — через УЗО или дифавтомат с током утечки не более 30 мА (ПУЭ 7.1.79); в санузле выполнить ДСУП (ПУЭ 7.1.87–7.1.88).
6. Кабель — медный, исполнение нг(А)-LS (ГОСТ 31565-2012); скрытая прокладка только горизонтально и вертикально, фактические трассы зафиксировать исполнительной схемой до закрытия отделкой.
7. Расчёт нагрузок, токов КЗ, селективности и сечений — по проекту ЭОМ организации с допуском СРО; лист задаёт состав, расположение и группы.
8. Расшифровка клавиш и ведомость изделий — лист 43.

1000 мм · печать 1:1

Изм.	Кол.уч	Лист	№ док.	Подп.	Дата
Разраб.		Кырлан А.С.			04.11.26
Пров.					
ГИП					
Н. контр.					
Утв.					

ГД-2026-010-АИ

Дом 331 м²

Общая площадь 270,67* м² · * размеры приняты, не замерены (реестр — л. 8–10, К-1)

Дизайн-проект интерьера

Стадия	Лист	Листов
РП	42	216

План выключателей и схема включения · Мансарда

М 1:75

Кырлан Александр Сергеевич

выпуск 04.11.2026 № 2a77323a49 · стр. 43 из 221

02

Электрооборудование

Кырлан Александр Сергеевич

выпуск 04.11.2026 № 2a77323a49 · стр. 44 из 221

Ведомость электроточек и изделий

Электроточки, изделия, светильники, освещённость, клавиши выключателей · б/м

Ведомость электроточек

Марка	Пом.	Назначение	Н, мм	Гр.
Р16	1	фартук: мелкая техника	1150	9
Р17	1	фартук: мелкая техника	1150	9
Р18	1	фартук: мелкая техника	1150	9
Р19	1	фартук: мелкая техника	1150	9
Р20	1	холодильник встроенный Кх5 (розетка в соседнем модуле)	150	10
Р21**	1	вытяжка над варочной панелью Кх3 (розетка за съёмной панелью)	2200	10
Р22	1	кухня: мелкая техника	300	10
Р23	1	уборка	300	10
Р24	1	торцевая панель острова Кх7: мелкая техника	150	10
Р25	1	торцевая панель острова Кх7: мелкая техника	150	10
Р26	1	посудомоечная машина в острове Кх7	150	16
ЭВ1**	1	вентилятор ВР1 (таймер выбега)	2550	1
ЭВ3	1	варочная панель Кх3	150	11
ЭВ4**	1	духовой шкаф Кх3 (вывод в соседнем модуле)	150	15
Р9	2	у кровати	600	7
Р10	2	у кровати	600	7
Р11	2	у комода	300	7
Р12**	2	ТВ над комодом (в одной зоне с ТВ2, LAN2)	1100	7
Р13	2	уборка	300	7
Р14	2	уборка у входа	300	7
КУП1**	3	КУП — уравнивание потенциалов (ДСУП)	300	
Р7**	3	стиральная машина, IP44	1000	12
Р8**	3	фен у умывальника, IP44	1000	13
ЭВ4**	3	вентилятор ВР1 (таймер выбега)	2403	3
ЭВ6**	3	полотенцесушитель П10, IP44	700	13
ЭВ9**	4	вывод питания котла и насосов	1200	21
Р1	5	ТВ-зона: телевизор, медиаплеер	950	5
Р2	5	ТВ-зона: саундбар	950	5
Р3	5	общего назначения	300	5

Ведомость электроточек (продолжение)

Марка	Пом.	Назначение	Н, мм	Гр.
Р4	5	кресло у окна Гс4	300	5
Р5	5	общего назначения	300	5
Р6	5	уборка	300	5
Р34	6	уборка	300	6
Р15	8	пылесос, сушилка обуви	300	6
Р39	8	уборка	300	6
Р40**	8	питание слаботочного щита (рядом с ЩС**)	1700	14
ЩК	8	щит квартирный ЩРВ-П-48	1700	
Р36**	10	верстак, электроинструмент	1100	20
Р37**	10	верстак, зарядка аккумуляторов	1100	20
Р38**	10	привод секционных ворот (под потолком у направляющей)	2400	20
Р35	11	балкон: розетка общего назначения, IP44	300	8
Р41	12	балкон: розетка общего назначения, IP44	300	8
Р42	13	у кровати	600	4
Р43	13	у кровати	600	4
Р44	13	рабочий стол	900	4
Р45	13	рабочий стол	900	4
Р46	13	торшер у кресла	300	4
Р47	13	уборка	300	4
КУП3**	15	КУП — уравнивание потенциалов (ДСУП)	300	
Р48**	15	стиральная машина, IP44	1000	12
Р49**	15	фен у умывальника, IP44	1000	13
ЭВ8**	15	вентилятор ВР1 (таймер выбега)	2403	3
ЭВ9**	15	полотенцесушитель П10, IP44	700	13
Р50	16	у кровати	600	17
Р51	16	у кровати	600	17
Р52	16	у комода	300	17
Р53**	16	ТВ над комодом (в одной зоне с ТВ3, LAN4)	1100	17
Р54	16	уборка	300	17
Р55	16	уборка у входа	300	17

Ведомость электроточек (продолжение)

Марка	Пом.	Назначение	Н, мм	Гр.
Р56	17	уборка	300	6
Р57	18	у кровати	600	18
Р58	18	у кровати	600	18
Р59	18	у комода	300	18
Р60**	18	ТВ над комодом (в одной зоне с ТВ4, LAN5)	1100	18
Р61	18	уборка	300	18
Р62	18	уборка у входа	300	18
Р63	19	у кровати	600	19
Р64	19	у кровати	600	19
Р65	19	у комода	300	19
Р66**	19	ТВ над комодом (в одной зоне с ТВ5, LAN6)	1100	19
Р67	19	уборка	300	19
Р68	19	уборка у входа	300	19
КУП2**	20	КУП — уравнивание потенциалов (ДСУП)	300	
Р33**	20	фен у умывальника, IP44	1000	13
ЭВ5**	20	вентилятор ВР3 (таймер выбега)	2343	3
ЭВ7**	20	полотенцесушитель П13, IP44	700	13

Ведомость изделий

Наименование	Марки	Ед.	Кол.
Розетка с з/к и защитными шторками, 16 А	по ведомости точек	шт	62
Розетка IP44 с крышкой, 16 А	Р7**, Р8**, Р33**, Р35, Р41, Р48**, Р49**	шт	7
Выключатель 1-клав.	S14, S17, S30, S31	шт	4
Выключатель 1-клав. перекрёстный	S11, S19	шт	2
Выключатель 1-клав. проходной	S10, S15, S16, S18, S26	шт	5
Выключатель 2-клав.	S32	шт	1
Выключатель 2-клав. (перекрёстная + обычная)	S20	шт	1
Выключатель 2-клав. (перекрёстная + проходная)	S21, S23, S28, S33	шт	4

Ведомость изделий (продолжение)

Наименование	Марки	Ед.	Кол.
Выключатель 2-клав. перекрёстный	S3–S6, S8, S13, S24, S27, S29–S31, S34	шт	12
Выключатель 2-клав. проходной	S1, S7, S12, S22, S25, S32	шт	6
Светорегулятор 1-канальный, задний фронт (LED)	S2**	шт	1
Датчик движения ночной подсветки	L11	шт	1
Рамка 1-постовая	в т. ч. 36 под выключ.	шт	91
Рамка 2-постовая		шт	7
Коробка установочная (подрозетник) Ø68	розетки, выключатели	шт	105
Вывод кабеля под прибор (клеммник)	ЭВ3, ЭВ4**, ЭВ5**, ЭВ6**, ЭВ7**, ЭВ8**, ЭВ9**	шт	9
Вывод кабеля к вентилятору вытяжки	ЭВ1**	шт	1
Коробка уравнивания потенциалов КУП	КУП1**, КУП2**, КУП3**	шт	3
Блок питания LED 24 В, 30 Вт	БП2	шт	1
Блок питания LED 24 В, 150 Вт, дим.	БП3	шт	1
Блок питания LED 24 В, 200 Вт, дим.	БП4, БП6–БП9	шт	5
Блок питания LED 24 В, 300 Вт, дим.	БП1	шт	1
Блок питания LED 24 В, 20 Вт	БП5	шт	1
Извещатель дымовой автономный	ИП1, ИП2, ИП3**, ИП6**, ИП7, ИП8, ИП9**, ИП10, ИП11, ИП12**	шт	10
Извещатель тепловой	ИП4	шт	1
Щит квартирный (состав — лист щита)	ЩК	шт	1
Розетка компьютерная RJ45, кат. 6, с рамкой и подрозетником	LAN1–LAN6, LAN7**	шт	7
Розетка телевизионная (коаксиальная) с рамкой и подрозетником	ТВ1–ТВ5	шт	5
Точка доступа Wi-Fi (оборудование заказчика), питание PoE	АР1**	шт	1
Трубка или монитор домофона (поставка домофонной организации)	ДФ1	шт	1
Щит слаботочный ЩС**: корпус, DIN-рейка, розетки 220 В	ЩС**	шт	1
Патч-панель, портов не менее 8		шт	1

Примечания

1. Ведомости сведены с планов розеток, освещения и выключателей; марки, группы и высоты — те же, что у знаков на планах.
2. Механизмы, рамки и светорегуляторы — одной серии; число постов и клавиш сверено с выбранной серией. Перекрёстная клавиша — отдельный механизм серии.
3. Освещённость (оценка) — по норме СанПиН 1.2.3685-21 (табл. 5.52, на полу), не светотехнический расчёт; декоративная подсветка в оценку не входит.
4. За отметку 0,000 принят уровень чистого пола. Высоты Н — от чистого пола до оси изделия; привязки — от чистовой грани стены до оси механизма (у рамки на несколько постов — до оси рамки).
5. Розеточные и мокрые линии — через УЗО или дифавтомат с током утечки не более 30 мА (ПУЭ 7.1.79); в санузле выполнить ДСУП (ПУЭ 7.1.87–7.1.88).
6. Кабель — медный, исполнение нг(А)-LS (ГОСТ 31565-2012); скрытая прокладка только горизонтально и вертикально, фактические трассы зафиксировать исполнительной схемой до закрытия отделкой.
7. Расчёт нагрузок, токов КЗ, селективности и сечений — по проекту ЭОМ организации с допуском СРО; лист задаёт состав, расположение и группы.
8. Ведомости занимают 3 листов этого наименования: таблицы, не вошедшие в поле листа, продолжены на следующем листе.

Допущения и предложения на листе. Знак «**» предложено (согласовать). См. лист открытых вопросов (листы 8–10).

Изм.	Кол.уч	Лист	№ док.	Подп.	Дата
Разраб.		Кырлан А.С.			04.11.26
Пров.					
ГИП					
Н. контр.					
Утв.					

ГД-2026-010-АИ

Дом 331 м²

Общая площадь 270,67* м² · * размеры приняты, не замерены (реестр — л. 8–10, К-1)

Дизайн-проект интерьера

Стадия	Лист	Листов
РП	43	216

Ведомость электроточек и изделий

М б/м

Кырлан Александр Сергеевич

выпуск 04.11.2026 № 2a77323a49 · стр. 45 из 221

Ведомость электроточек и изделий (продолжение)

Электроточки, изделия, светильники, освещённость, клавиши выключателей · б/м

Ведомость изделий (продолжение)

Наименование	Марки	Ед.	Кол.
Коммутатор, портов не менее 8, из них PoE 1		шт	1
Кабель домофона — тип по системе поставщика (по лучам от ЩС**, запас 10 %)		м	2,8
Кабель коаксиальный RG-6 (75 Ом) к розеткам ТВ (по лучам от ЩС**, запас 10 %)		м	70,6
Кабель U/UTP кат. 5e (LAN, Wi-Fi и камеры по PoE) (по лучам от ЩС**, запас 10 %)		м	11,9
Кабель U/UTP кат. 6 (LAN, Wi-Fi и камеры по PoE) (по лучам от ЩС**, запас 10 %)		м	96,4

Ведомость светильников

Поз.	Марки	Тип	Кол.	P, Вт	Ф, лм	IP	Тц/Ra
1	Св1–Св8, Св31–Св37	встраиваемый точечный	15	12	1000		3000/90
2	Св38, Св39	линейный светильник	2	8	700		3000/90
3	Св40	светодиодная лента, 10,2 м	1	97,9	9180		2700/90
4	Св17–Св22, Св76–Св81, Св87–Св92, Св96–Св101	встраиваемый точечный	24	12	1050		2700/90
5	Св23	светодиодная лента, 5,4 м	1	51,8	4860		2700/90
6	Св11, Св24, Св25, Св70, Св83, Св84, Св94, Св95, Св103, Св104	настенный (бра), H=1500	10	6	400		2700/90
7	Св12–Св14, Св51, Св72–Св74	встраиваемый точечный	7	6	500	44	3000/90
8	Св15**, Св52**, Св75**	настенный (бра), H=1900	3	8	600	44	3000/90
9	Св16, Св55, Св58, Св71	потолочный накладной	4	10	900		3000/90
10	Св9	подвесной	1	15	1200		2700/90
11	Св10	светодиодная лента, 21,1 м	1	202,6	18990		2700/90

Ведомость светильников (продолжение)

Поз.	Марки	Тип	Кол.	P, Вт	Ф, лм	IP	Тц/Ra
12	Св26–Св29, Св53, Св54, Св85, Св86	встраиваемый точечный	8	7	600		3000/90
13	Св30**	светодиодная лента, 1,8 м	1	8,6	270		2700/90
14	Св56, Св57	потолочный накладной	2	24	2500		3000/90
15	Св59**, Св60**	потолочный накладной	2	9	800	44	3000/90
16	Св61–Св68	встраиваемый точечный	8	12	1000		2700/90
17	Св69, Св102	светодиодная лента, 6 м	2	57,6	5400		2700/90
18	Св82	светодиодная лента, 3,2 м	1	30,7	2880		2700/90
19	Св93	светодиодная лента, 15,5 м	1	148,8	13950		2700/90
20	Св50	встраиваемый точечный	1	7	600	44	3000/90

Освещённость (оценка)

Пом.	S, м²	Ен, лк	Ф треб., лм	Ф по пр., лм
1	24,6	150	10390	7000
2	11,9	300	10070	6300
3	4,9	50	690	1500
4	6,9	30	580	900
5	33,7	150	14260	8000
6	10	50	1410	1200
7	6	30	510	900
8	12,5	50	1750	2400
9	3,5	50	490	900
10	41,6	30	3510	5000
13	24,6	150	10390	8000
14	6,7	75	1420	900
15	6,9	50	970	1500
16	15,5	150	6560	6300
17	21,7	50	3060	1200
18	17,1	200	9640	6300
19	16,3	200	9170	6300
20	6,3	50	890	1100

Расшифровка клавиш

Марка	Пом.	H, мм	Клав.	Механизм	Группа: светильники
S1	5	900	1	проходной	L1: Св1–Св8, Св61–Св68
			2	проходной	L2: Св9, Св69
S2**	5	900	1	светорегулятор	L3: Св10, Св11, Св70
S3	13	800	1	перекрёстный	L1: Св1–Св8, Св61–Св68
			2	перекрёстный	L3: Св10, Св11, Св70
S4	2	900	1	перекрёстный	L7: Св17–Св22, Св76–Св81, Св87–Св92, Св96–Св101
			2	перекрёстный	L8: Св23, Св82, Св93, Св102
S5	2	800	1	перекрёстный	L7: Св17–Св22, Св76–Св81, Св87–Св92, Св96–Св101
			2	перекрёстный	L9: Св24, Св25, Св83, Св84, Св94, Св95, Св103, Св104
S6	2	800	1	перекрёстный	L7: Св17–Св22, Св76–Св81, Св87–Св92, Св96–Св101
			2	перекрёстный	L9: Св24, Св25, Св83, Св84, Св94, Св95, Св103, Св104
S7	1	900	1	проходной	L4: Св12–Св14, Св31–Св37, Св72–Св74 + ЭВ1** (вентилятор)
			2	проходной	L5: Св15**, Св38, Св39, Св75**
S8	1	900	1	перекрёстный	L4: Св12–Св14, Св31–Св37, Св72–Св74 + ЭВ1** (вентилятор)
			2	перекрёстный	L5: Св15**, Св38, Св39, Св75**
S10	1	900	1	проходной	L6: Св16, Св40, Св71
S11	6	900	1	перекрёстный	L10: Св26–Св29, Св53, Св54, Св85, Св86
S12	6	900	1	проходной	L4: Св12–Св14, Св31–Св37, Св72–Св74 + ЭВ1** (вентилятор)
			2	проходной	L5: Св15**, Св38, Св39, Св75**
S13	6	900	1	перекрёстный	L6: Св16, Св40, Св71
			2	перекрёстный	L10: Св26–Св29, Св53, Св54, Св85, Св86
S14	9	900	1	обычный	L19: Св55

Расшифровка клавиш (продолжение)

Марка	Пом.	H, мм	Клав.	Механизм	Группа: светильники
S15	10	900	1	проходной	L20: Св56, Св57
S16	10	900	1	проходной	L20: Св56, Св57
S17	4	900	1	обычный	L21: Св58
S18	8	900	1	проходной	L10: Св26–Св29, Св53, Св54, Св85, Св86
S19	8	900	1	перекрёстный	L10: Св26–Св29, Св53, Св54, Св85, Св86
S20	8	900	1	перекрёстный	L10: Св26–Св29, Св53, Св54, Св85, Св86
			2	обычный	L11: Св30**
S21	13	900	1	перекрёстный	L1: Св1–Св8, Св61–Св68
			2	проходной	L2: Св9, Св69
S22	13	800	1	проходной	L1: Св1–Св8, Св61–Св68
			2	проходной	L3: Св10, Св11, Св70
S23	16	900	1	перекрёстный	L7: Св17–Св22, Св76–Св81, Св87–Св92, Св96–Св101
			2	проходной	L8: Св23, Св82, Св93, Св102
S24	16	800	1	перекрёстный	L7: Св17–Св22, Св76–Св81, Св87–Св92, Св96–Св101
			2	перекрёстный	L9: Св24, Св25, Св83, Св84, Св94, Св95, Св103, Св104
S25	16	800	1	проходной	L7: Св17–Св22, Св76–Св81, Св87–Св92, Св96–Св101
			2	проходной	L9: Св24, Св25, Св83, Св84, Св94, Св95, Св103, Св104
S26	17	900	1	проходной	L10: Св26–Св29, Св53, Св54, Св85, Св86
S27	17	900	1	перекрёстный	L4: Св12–Св14, Св31–Св37, Св72–Св74 + ЭВ1** (вентилятор)
			2	перекрёстный	L5: Св15**, Св38, Св39, Св75**
S28	17	900	1	проходной	L6: Св16, Св40, Св71
			2	перекрёстный	L10: Св26–Св29, Св53, Св54, Св85, Св86

Примечания

1. Продолжение ведомостей: лист 2 из 3 этого наименования; таблицы, прерванные на предыдущем листе, продолжены с заголовком «(продолжение)».
2. За отметку 0,000 принят уровень чистого пола. Высоты H — от чистого пола до оси изделия; привязки — от чистовой грани стены до оси механизма (у рамки на несколько постов — до оси рамки).
3. Розеточные и мокрые линии — через УЗО или дифавтомат с током утечки не более 30 мА (ПУЭ 7.1.79); в санузле выполнить ДСУП (ПУЭ 7.1.87–7.1.88).
4. Кабель — медный, исполнение нг(A)-LS (ГОСТ 31565-2012); скрытая прокладка только горизонтально и вертикально, фактические трассы зафиксировать исполнительной схемой до закрытия отделкой.
5. Расчёт нагрузок, токов КЗ, селективности и сечений — по проекту ЭОМ организации с допуском СРО; лист задаёт состав, расположение и группы.

Допущения и предложения на листе. Основа листа: размеры и контуры этажей подобраны проектировщиком по составу помещений и площадям этажей с картинки 470 px (размеры на ней не читаются); обмер и исходный проект — задание (К-1); высоты: 1-й этаж 2800 мм, мансарда 2700 мм (горизонтальная часть) приняты; скаты кровли мансарды приняты по картинке: колено 1200 мм, уклон 45°, конёк вдоль длинной стороны; проект КР — задание (К-2); наружные стены 400 мм, перегородки 120 мм приняты (К-1); разрешённая мощность 15 кВт принята по типовым ТУ для частного дома (К-4); подрайон климата не задан — принят не северный (жилые от 2,5 м) (К-7). Знак «**» — предложено, не утверждено (согласовать): Св15, S2, Св30, Св75, ЩС, ЭВ1; ИЗ-1: Св59, Св60, Св52. См. лист открытых вопросов (лист 8, записи К-1, К-2, К-4, К-7; лист 10, запись ИЗ-1).

Изм.	Кол.уч	Лист	№ док.	Подп.	Дата
Разраб.		Кырлан А.С.			04.11.26
Пров.					
ГИП					
Н. контр.					
Утв.					

ГД-2026-010-АИ

Дом 331 м²

Общая площадь 270,67* м² · * размеры приняты, не замерены (реестр — л. 8–10, К-1)

Дизайн-проект интерьера

Стадия	Лист	Листов
РП	44	216

Ведомость электроточек и изделий (продолжение)

М б/м

Кырлан Александр Сергеевич

Ведомость электроточек и изделий (продолжение)

Электроточки, изделия, светильники, освещённость, клавиши выключателей · б/м

Расшифровка клавиш (продолжение)

Марка	Пом.	Н, мм	Клав.	Механизм	Группа: светильники
S29	18	900	1	перекрёстный	L7: Св17–Св22, Св76–Св81, Св87–Св92, Св96–Св101
			2	перекрёстный	L8: Св23, Св82, Св93, Св102
S30	5	900	1	обычный	L12: Св59**
S30	18	800	1	перекрёстный	L7: Св17–Св22, Св76–Св81, Св87–Св92, Св96–Св101
			2	перекрёстный	L9: Св24, Св25, Св83, Св84, Св94, Св95, Св103, Св104
S31	9	900	1	обычный	L13: Св60**
S31	18	800	1	перекрёстный	L7: Св17–Св22, Св76–Св81, Св87–Св92, Св96–Св101
			2	перекрёстный	L9: Св24, Св25, Св83, Св84, Св94, Св95, Св103, Св104
S32	17	900	1	обычный	L17: Св50, Св51
			2	обычный	L18: Св52**
S32	19	900	1	проходной	L7: Св17–Св22, Св76–Св81, Св87–Св92, Св96–Св101
			2	проходной	L8: Св23, Св82, Св93, Св102
S33	19	800	1	перекрёстный	L7: Св17–Св22, Св76–Св81, Св87–Св92, Св96–Св101
			2	проходной	L9: Св24, Св25, Св83, Св84, Св94, Св95, Св103, Св104
S34	19	800	1	перекрёстный	L7: Св17–Св22, Св76–Св81, Св87–Св92, Св96–Св101
			2	перекрёстный	L9: Св24, Св25, Св83, Св84, Св94, Св95, Св103, Св104

Допущения и предложения на листе

Основа листа: размеры и контуры этажей подобраны проектировщиком по составу помещений и площадям этажей с картинки 470 px (размеры на ней не читаются); обмер и исходный проект — задание (К-1); высоты: 1-й этаж 2800 мм, мансарда 2700 мм (горизонтальная часть) приняты; скаты кровли мансарды приняты по картинке: колено 1200 мм, уклон 45°, конёк вдоль длинной стороны; проект КР — задание (К-2); наружные стены 400 мм, перегородки 120 мм приняты (К-1); разрешённая мощность 15 кВт принята по типовым ТУ для частного дома (К-4); подрайон климата не задан — принят не северный (жилые от 2,5 м) (К-7).

Знак «**» — предложение проектировщика, заказчиком не утверждено (согласовать с заказчиком): ИЗ-1: Св59, Св60 — накладной вместо встраиваемого: потолок окрашенный, без подвесной конструкции (летнее помещение) — корпусу встраиваемого негде стоять; Св52 — Сдвиг под раскладку плитки стены Б на 25 мм вдоль стены — ось на шве или в центре плитки, привязка по таблице листа.

См. лист открытых вопросов (лист 8, записи К-1, К-2, К-4, К-7; лист 10, запись ИЗ-1).

Примечания

1. Продолжение ведомостей: лист 3 из 3 этого наименования; таблицы, прерванные на предыдущем листе, продолжены с заголовком «(продолжение)».
2. За отметку 0,000 принят уровень чистого пола. Высоты Н — от чистого пола до оси изделия; привязки — от чистовой грани стены до оси механизма (у рамки на несколько постов — до оси рамки).
3. Розеточные и мокрые линии — через УЗО или дифавтомат с током утечки не более 30 мА (ПУЭ 7.1.79); в санузле выполнить ДСУП (ПУЭ 7.1.87–7.1.88).
4. Кабель — медный, исполнение нг(А)-LS (ГОСТ 31565-2012); скрытая прокладка только горизонтально и вертикально, фактические трассы зафиксировать исполнительной схемой до закрытия отделкой.
5. Расчёт нагрузок, токов КЗ, селективности и сечений — по проекту ЭОМ организации с допуском СРО; лист задаёт состав, расположение и группы.

Изм.	Кол.уч	Лист	№ док.	Подп.	Дата
Разраб.		Кырлан А.С.			04.11.26
Пров.					
ГИП					
Н. контр.					
Утв.					

ГД-2026-010-АИ

Дом 331 м²

Общая площадь 270,67* м² · * размеры приняты, не замерены (реестр — л. 8–10, К-1)

Дизайн-проект интерьера

Стадия	Лист	Листов
РП	45	216


Ведомость электроточек и изделий (продолжение)

М б/м

Кырлан Александр Сергеевич

Однолинейная схема щита

Щит квартирный ЩК · гр. 1—11 из 21 · без масштаба

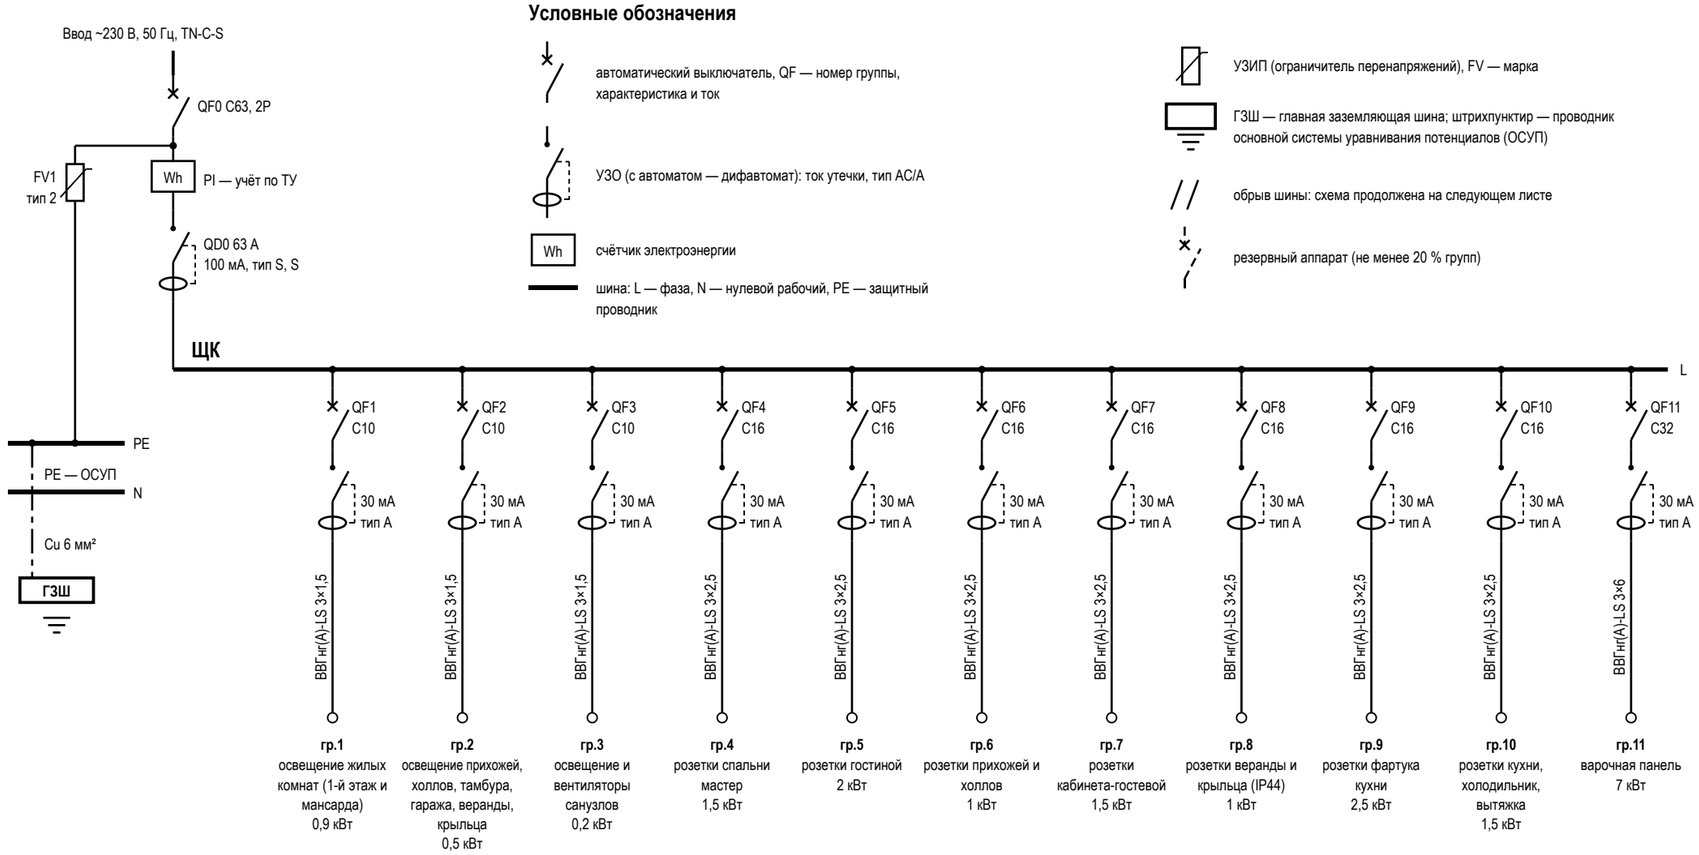

Условные обозначения

- автоматический выключатель, QF — номер группы, характеристика и ток
- УЗО (с автоматом — дифавтомат): ток утечки, тип AC/A
- Wh — счётчик электроэнергии
- шина: L — фаза, N — нулевой рабочий, PE — защитный проводник
- УЗИП (ограничитель перенапряжений), FV — марка
- ГЗШ — главная заземляющая шина; штрихпунктир — проводник основной системы уравнивания потенциалов (ОСУП)
- обрыв шины: схема продолжена на следующем листе
- резервный аппарат (не менее 20 % групп)

Данные щитка

Показатель	Значение
Номер щитка	ЩК
Тип	ЩРВ-П-72, IP41
Уст. мощность, кВт	36,1
Разреш. мощность, кВт	15
Расчётная, кВт	13,8
Автоматы 1п: занят. / рез.	21 / 5
Модулей: всего / занято	72 / 48
Ток на вводе, А	63
Вводной аппарат	QF0 C63, 2P
УЗИП	FV1, тип 2, ЩК, после счётчика
ГЗШ, проводник ОСУП	Cu 6 мм²
Листов схемы	2 (группы по листам)

Таблица групп щита ЩК и кабельный журнал

№	Назначение	Помещения	Автомат	УЗО / дифавтомат	Кабель	Длина, м	Р, кВт	Точек
1	освещение жилых комнат (1-й этаж и мансарда)	1, 2, 5, 6, 7, 13, 14, 16, 17, 18, 19	C10	30 мА, тип A	ВВГнг(A)-LS 3×1,5	387,2	0,9	99
2	освещение прихожей, холлов, тамбура, гаража, веранды, крыльца	4, 5, 6, 8, 9, 10, 11, 12, 17	C10	30 мА, тип A	ВВГнг(A)-LS 3×1,5	157,7	0,5	27
3	освещение и вентиляторы санузлов	3, 6, 15, 17, 20	C10	30 мА, тип A	ВВГнг(A)-LS 3×1,5	84,7	0,2	17
4	розетки спальни мастер	13	C16	30 мА, тип A	ВВГнг(A)-LS 3×2,5	37,7	1,5	6
5	розетки гостиной	5	C16	30 мА, тип A	ВВГнг(A)-LS 3×2,5	33,5	2	6
6	розетки прихожей и холлов	6, 8, 17	C16	30 мА, тип A	ВВГнг(A)-LS 3×2,5	22	1	4
7	розетки кабинета-гостевой	2	C16	30 мА, тип A	ВВГнг(A)-LS 3×2,5	24,9	1,5	6
8	розетки веранды и крыльца (IP44)	11, 12	C16	30 мА, тип A	ВВГнг(A)-LS 3×2,5	35	1	2
9	розетки фартука кухни	1	C16	30 мА, тип A	ВВГнг(A)-LS 3×2,5	32,1	2,5	4
10	розетки кухни, холодильник, вытяжка	1	C16	30 мА, тип A	ВВГнг(A)-LS 3×2,5	33,6	1,5	6
11	варочная панель	1	C32	30 мА, тип A	ВВГнг(A)-LS 3×6	23,6	7	1

Допущения и предложения на листе

Основа листа: размеры и контуры этажей подобраны проектировщиком по составу помещений и площадям этажей с картинки 470 px (размеры на ней не читаются); обмер и исходный проект — задание (К-1); высоты: 1-й этаж 2800 мм, мансарда 2700 мм (горизонтальная часть) приняты; скаты кровли мансарды приняты по картинке: колено 1200 мм, уклон 45°, конёк вдоль длинной стороны; проект КР — задание (К-2); наружные стены 400 мм, перегородки 120 мм приняты (К-1); разрешённая мощность 15 кВт принята по типовым ТУ для частного дома (К-4); подрайон климата не задан — принят не северный (жилые от 2,5 м) (К-7).

Открытые вопросы и конфликты по листу: К-4.

См. лист открытых вопросов (лист 8, записи К-1, К-2, К-4, К-7).

Примечания

1. Схема однолинейная: одна линия — фаза, N и PE группы; аппараты — в отключённом положении (ГОСТ 2.702, ГОСТ 2.755). Номера групп — как у точек на планах (гр.). За отметку 0,000 принят уровень чистого пола; высота щита — по плану розеток.
2. Розеточные и мокрые линии — через УЗО или дифавтомат с током утечки не более 30 мА (ПУЭ 7.1.79); в санузле выполнить ДСУП (ПУЭ 7.1.87–7.1.88).
3. УЗО тип A — для линий с электроникой, стиральной и посудомоечной машиной, LED-драйверами; тип AC — только для чисто активной нагрузки.
4. Кабель — медный, исполнение нг(A)-LS (ГОСТ 31565-2012); скрытая прокладка только горизонтально и вертикально, фактические трассы зафиксировать исполнительной схемой до закрытия отделкой.
5. Номинал автомата — не выше допустимого тока кабеля: 1,5 мм² — до 10 А, 2,5 мм² — до 16 А. Резерв щита — не менее 20 % модулей.
6. Расчёт нагрузок, токов КЗ, селективности и сечений — по проекту ЭОМ организации с допуском СРО; лист задаёт состав, расположение и группы.
7. УЗИП FV1 — после вводного автомата, проводник к шине PE — кратчайший, без петель. Шина PE щита соединяется с ГЗШ проводником ОСУП; к ГЗШ присоединяются трубы водопровода и отопления на вводе в квартиру (ПУЭ 7.1.87). Шины N и PE — раздельные, после разделения PEN не объединяются.
8. До подключения нагрузки — приёмо-сдаточные испытания с протоколом: сопротивление изоляции линий не менее 0,5 МОм, срабатывание УЗО по току и времени, непрерывность защитных проводников PE (ПУЭ, гл. 1.8).

Изм.	Кол.уч	Лист	№ док.	Подп.	Дата
Разраб.		Кырлан А.С.			04.11.26
Пров.					
ГИП					
Н. контр.					
Утв.					

ГД-2026-010-АИ

Дом 331 м²

Общая площадь 270,67* м² · * размеры приняты, не замерены (реестр — л. 8–10, К-1)

Дизайн-проект интерьера

Стадия	Лист	Листов
РП	46	216

Однолинейная схема щита

М б/м

Кырлан Александр Сергеевич

выпуск 04.11.2026 № 2a7323a49 · стр. 48 из 221

Однолинейная схема щита (продолжение)

Щит квартирный ЩК · гр. 12—21 из 21 · без масштаба

Продолжение однолинейной схемы щита ЩК, начало — лист 46

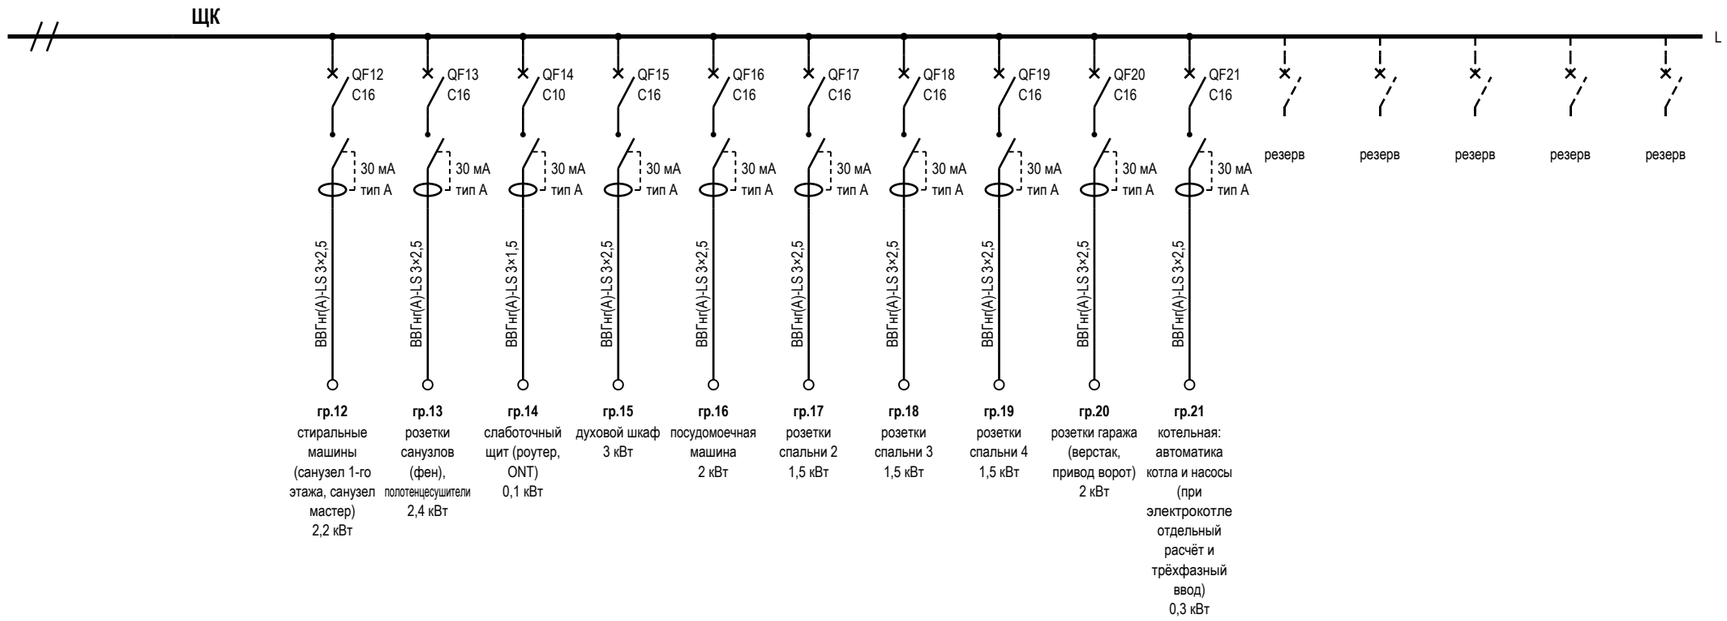


Таблица групп щита ЩК и кабельный журнал (продолжение)

№	Назначение	Помещения	Автомат	УЗО / дифавтомат	Кабель	Длина, м	P, кВт	Точек
12	стиральные машины (санузел 1-го этажа, санузел мастер)	3, 15	C16	30 мА, тип A	ВВГнг(A)-LS 3×2,5	22,8	2,2	2
13	розетки санузлов (фен), полотенцесушители	3, 15, 20	C16	30 мА, тип A	ВВГнг(A)-LS 3×2,5	57,5	2,4	6
14	слаботочный щит (роутер, ONT)	8	C10	30 мА, тип A	ВВГнг(A)-LS 3×1,5	3,8	0,1	1
15	духовой шкаф	1	C16	30 мА, тип A	ВВГнг(A)-LS 3×2,5	22,7	3	1
16	посудомоечная машина	1	C16	30 мА, тип A	ВВГнг(A)-LS 3×2,5	16,2	2	1
17	розетки спальни 2	16	C16	30 мА, тип A	ВВГнг(A)-LS 3×2,5	25,7	1,5	6
18	розетки спальни 3	18	C16	30 мА, тип A	ВВГнг(A)-LS 3×2,5	29,7	1,5	6
19	розетки спальни 4	19	C16	30 мА, тип A	ВВГнг(A)-LS 3×2,5	29,8	1,5	6
20	розетки гаража (верстак, привод ворот)	10	C16	30 мА, тип A	ВВГнг(A)-LS 3×2,5	23,9	2	3
21	котельная: автоматика котла и насосы (при электрокотле отдельный расчёт и трёхфазный ввод)	4	C16	30 мА, тип A	ВВГнг(A)-LS 3×2,5	16,2	0,3	1
	Итого по сечениям ВВГнг(A)-LS (все группы щита), м: 3×1,5 — 633,4; 3×2,5 — 463,3; 3×6 — 23,6					1120,3		

Примечания

1. Лист — продолжение однолинейной схемы щита ЩК: начало, данные щитка и условные обозначения — лист 46. Ввод, учёт, вводной аппарат, УЗИП, шины N и PE и ГЗШ показаны там же; шина L листа — та же шина щита.
2. Схема однолинейная: одна линия — фаза, N и PE группы; аппараты — в отключённом положении (ГОСТ 2.702, ГОСТ 2.755). Номера групп — как у точек на планах (гр.). За отметку 0,000 принят уровень чистого пола; высота щита — по плану розеток.
3. Розеточные и мокрые линии — через УЗО или дифавтомат с током утечки не более 30 мА (ПУЭ 7.1.79); в санузле выполнить ДСУП (ПУЭ 7.1.87–7.1.88).
4. УЗО тип A — для линий с электроникой, стиральной и посудомоечной машиной, LED-драйверами; тип AC — только для чисто активной нагрузки.
5. Кабель — медный, исполнение нг(A)-LS (ГОСТ 31565-2012); скрытая прокладка только горизонтально и вертикально, фактические трассы зафиксировать исполнительной схемой до закрытия отделкой.
6. Номинал автомата — не выше допустимого тока кабеля: 1,5 мм² — до 10 А, 2,5 мм² — до 16 А. Резерв щита — не менее 20 % модулей.
7. Расчёт нагрузок, токов КЗ, селективности и сечений — по проекту ЭОМ организации с допуском СРО; лист задаёт состав, расположение и группы.
8. До подключения нагрузки — приёмо-сдаточные испытания с протоколом: сопротивление изоляции линий не менее 0,5 МОм, срабатывание УЗО по току и времени, непрерывность защитных проводников PE (ПУЭ, гл. 1.8).

Допущения и предложения на листе

Основа листа: размеры и контуры этажей подобраны проектировщиком по составу помещений и площадям этажей с картинки 470 px (размеры на ней не читаются); обмер и исходный проект — задание (К-1); высоты: 1-й этаж 2800 мм, мансарда 2700 мм (горизонтальная часть) приняты; скаты кровли мансарды приняты по картинке: колено 1200 мм, уклон 45°, конёк вдоль длинной стороны; проект КР — задание (К-2); наружные стены 400 мм, перегородки 120 мм приняты (К-1); разрешённая мощность 15 кВт принята по типовым ТУ для частного дома (К-4); подрайон климата не задан — принят не северный (жилые от 2,5 м) (К-7).
См. лист открытых вопросов (лист 8, записи К-1, К-2, К-4, К-7).

Изм.	Кол.уч	Лист	№ док.	Подп.	Дата	ГД-2026-010-АИ		
						Дом 331 м²		
						Общая площадь 270,67* м² · * размеры приняты, не замерены (реестр — л. 8–10, К-1)		
Разраб.		Кырлан А.С.			04.11.26	Дизайн-проект интерьера	Стадия: РП	Лист: 47 / Листов: 216
Пров.								
ГИП								
Н. контр.						Однолинейная схема щита (продолжение) М б/м	Кырлан Александр Сергеевич	
Утв.								

выпуск 04.11.2026 № 2a77323a49 · стр. 49 из 221

План принципиальных трасс · 1-й этаж

Силовые трассы и объёмы электромонтажа, слаботочка в объёмах · размеры в мм


ПРЕДВАРИТЕЛЬНО · не для производства работ · открыто пунктов: 15 (реестр — л. 8–10)

Допущения и предложения на листе

Основа листа: размеры и контуры этажей подобраны проектировщиком по составу помещений и площадям этажей с картинки 470 px (размеры на ней не читаются); обмер и исходный проект — задание (К-1); высоты: 1-й этаж 2800 мм, мансарда 2700 мм (горизонтальная часть) приняты; скаты кровли мансарды приняты по картинке: колено 1200 мм, уклон 45°, конёк вдоль длинной стороны; проект КР — задание (К-2); наружные стены 400 мм, перегородки 120 мм приняты (К-1); разрешённая мощность 15 кВт принята по типовым ТУ для частного дома (К-4); подрайон климата не задан — принят не северный (жилые от 2,5 м) (К-7).

Знак «**» — предложение проектировщика, заказчиком не утверждено (согласовать с заказчиком): ЩС — щит слаботочный: место и состав; дверь пом. 8 (стена Б) — дверь гаража в дом — СП 55.13330.2016 п. 7.7: EI 30, уплотнение в притворах, самозакрывание (доводчик); К-9: дверь пом. 5 (стена В) — проём 2400×2100 на веранду с картинки: одной распашной створкой не закрывается (полотна 600–900) — раздвижная двустворчатая, остеклённая; система и полотна — по каталогу после утверждения автором.

См. лист открытых вопросов (лист 8, записи К-1, К-2, К-4, К-7; лист 9, запись К-9).

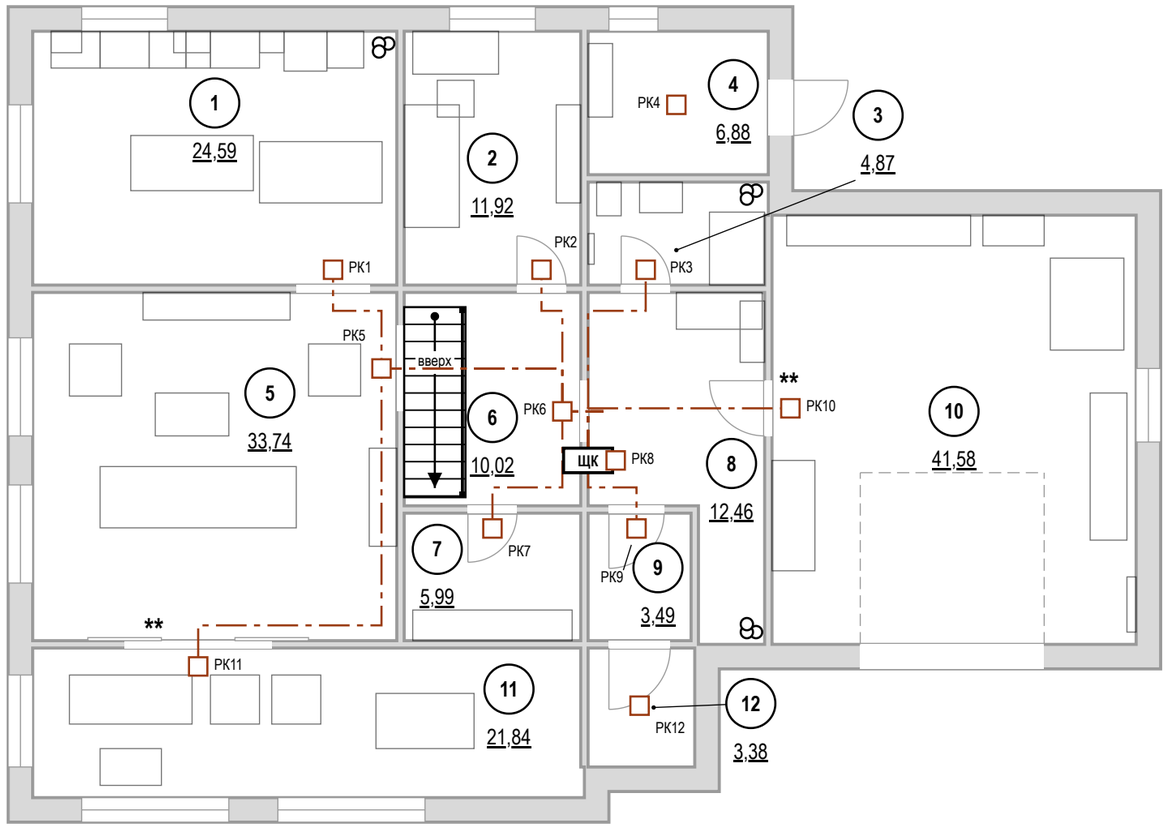

Кабель по группам ВВГнг(А)-LS, м

Гр.	мм²	Трасса	Данные
1	3×1,5	144	387,2
2	3×1,5	140,3	157,7
3	3×1,5	25,6	84,7
5	3×2,5	33,5	33,5
6	3×2,5	13,3	22
7	3×2,5	24,9	24,9
8	3×2,5	35	35
9	3×2,5	32,1	32,1
10	3×2,5	33,6	33,6

Гр.	мм²	Трасса	Данные
11	3×6	23,6	23,6
12	3×2,5	12,3	22,8
13	3×2,5	14,1	57,5
14	3×1,5	3,8	3,8
15	3×2,5	22,7	22,7
16	3×2,5	16,2	16,2
20	3×2,5	23,9	23,9
21	3×2,5	16,2	16,2
Σ		**615,1**	**1120,3**

Экспликация помещений

№	Помещение	Площадь, м²
1	Кухня-столовая	24,59
2	Кабинет-гостевая	11,92
3	Санузел 1 этажа	4,87
4	Котельная	6,88
5	Гостиная	33,74
6	Холл с лестницей	10,02
7	Кладовая	5,99
8	Прихожая	12,46
9	Тамбур	3,49
10	Гараж	41,58
11	Веранда *	21,84
12	Крыльцо *	3,38
	Итого по этажу	155,54
	Итого по дому	270,67

Объёмы прокладки

Работа, материал	Ед.	Кол.
Гофротруба Ø20 в потолочном пространстве	м	269,7
Кабель-канал плинтуса для силовых линий	м	164
Короб или накладной канал для вертикальных спусков и подъёмов	м	94,3
Коробка распределительная (РК) над дверью помещения	шт	12
Слаботочка: кабель домофона	м	2,8
Слаботочка: Кабель коаксиальный RG-6 (75 Ом) к розеткам ТВ	м	30
Слаботочка: Кабель U/UTP кат. 5е (LAN, Wi-Fi и камеры по PoE)	м	11,9
Слаботочка: U/UTP кат. 6 (LAN, Wi-Fi, камеры)	м	33,4
Слаботочка: гофротруба Ø20 отдельно от силовых	м	70,3

Штробы — только после заключения

Работа	Ед.	Кол.
Вертикальные штробы 20×20 мм от потолка до каждой настенной точки (в маршрут без штроб не входят)	м	112,77

Условные обозначения

- ЩК — щит квартирный
- РК — распределительная коробка над дверью помещения
- магистраль от щита к РК: потолочное пространство, гофра
- мебель и сантехприборы — подложка

Примечания

1. За отметку 0,000 принят уровень чистого пола. Высоты Н — от чистого пола до оси изделия; привязки — от чистовой грани стены до оси механизма (у рамки на несколько постов — до оси рамки).
2. Розеточные и мокрые линии — через УЗО или дифавтомат с током утечки не более 30 мА (ПУЭ 7.1.79); в санузле выполнить ДСУП (ПУЭ 7.1.87–7.1.88).
3. Кабель — медный, исполнение нг(А)-LS (ГОСТ 31565-2012); скрытая прокладка только горизонтально и вертикально, фактические трассы зафиксировать исполнительной схемой до закрытия отделкой.
4. Расчёт нагрузок, токов КЗ, селективности и сечений — по проекту ЭОМ организации с допуском СРО; лист задаёт состав, расположение и группы.
5. Длины — по плану: от щита вверх в потолочное пространство, по дверям и коридору без захода в мокрые помещения к распределительной коробке над дверью, далее к точкам; вертикали считаются вниз и обратно (у последней точки цепочки — в один конец); запас 10 %. Трассы принципиальные: фактическую зафиксировать исполнительной схемой до закрытия отделкой.
6. Несущие стены не определены: штробы в стенах не выполнять. Маршрут проложен без штроб: горизонтали — за потолком в гофре (269,7 м) и в кабель-канале плинтуса (164 м), вертикали — в коробе или накладном канале (166 м кабеля). Точек: за потолком — 47, спуск из потолка — 10, по плинтусу — 20, плинтус и подъём — 35.
7. Вариант со штробами — работа после технического заключения: 112,77 м вертикальных штроб от потолка до каждой настенной точки; условие — только после технического заключения: стена не несущая (или вертикальная штроба в несущей согласована конструктором), глубина и ширина 20–25 мм, не в зонах 0–2 ванной. Без заключения и согласования конструктора в смету и в график эта работа не входит.
8. В данных проекта (журнал щита) длины кабеля внесены оценкой (1120 м), по трассам из геометрии — 615 м (-45 %): к закупке и в смету принимать длины по трассам, а оценку в данных проекта заменить.
9. Слаботочные сети: кабели и точки считаются по лучам от ЩС** (лист слаботочных сетей): 78 м, портов патч-панели и коммутатора не менее 4; из точек 2 предложения листа слаботочки, не подтверждённые заказчиком. Изделия — в ведомости изделий.

1000 мм · печать 1:1

Изм.	Кол.уч	Лист	№ док.	Подп.	Дата
Разраб.		Кырлан А.С.			04.11.26
Пров.					
ГИП					
Н. контр.					
Утв.					

ГД-2026-010-АИ

Дом 331 м²

Общая площадь 270,67* м² · * размеры приняты, не замерены (реестр — л. 8–10, К-1)

Дизайн-проект интерьера	Стадия	Лист	Листов
	РП	48	216

План принципиальных трасс · 1-й этаж

М 1:100


Кырлан Александр Сергеевич

выпуск 04.11.2026 № 2a77323a49 · стр. 50 из 221

План принципиальных трасс · Мансарда

Силовые трассы и объёмы электромонтажа, слаботочка в объёмах · размеры в мм

ПРЕДВАРИТЕЛЬНО · не для производства работ · открыто пунктов: 15 (реестр — л. 8–10)

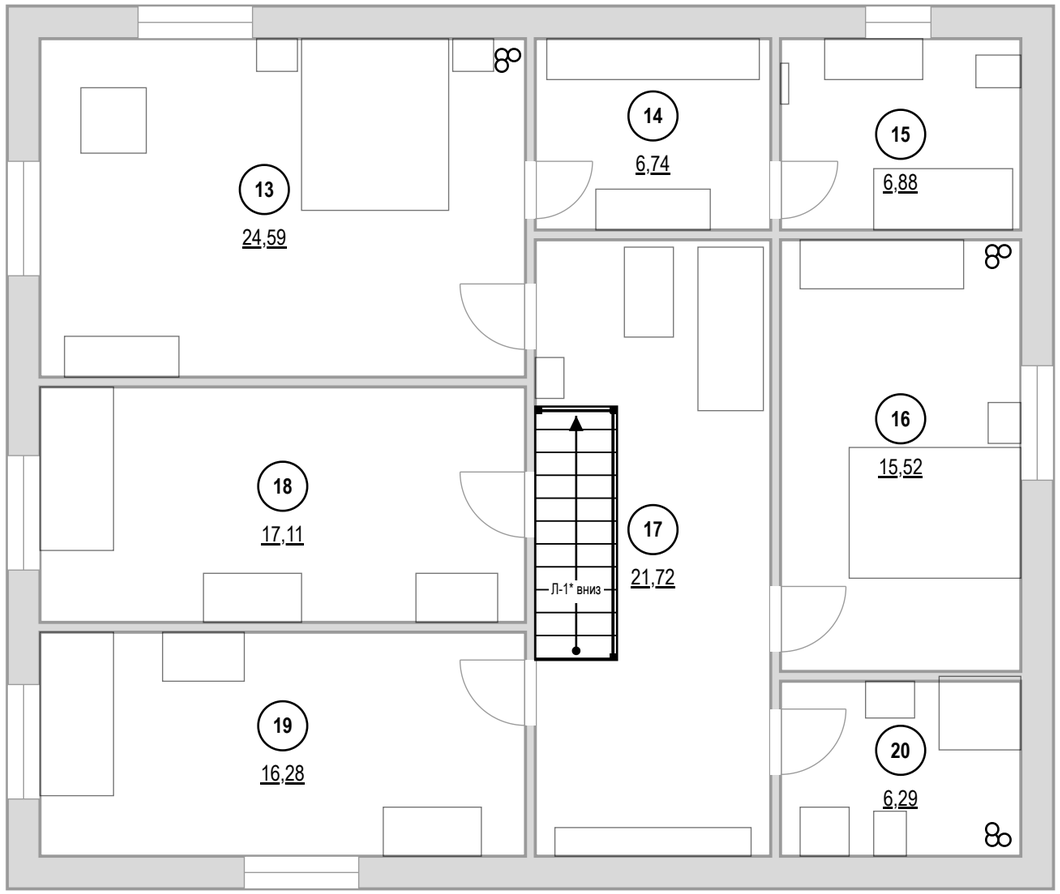

Трассы не построены

нет точки щита квартирного (points kind: panel) — трассу строить не от чего

Экспликация помещений

№	Помещение	Площадь, м²
13	Спальня мастер	24,59
14	Гардеробная мастер	6,74
15	Санузел мастер	6,88
16	Спальня 2	15,52
17	Холл мансарды	21,72
18	Спальня 3	17,11
19	Спальня 4	16,28
20	Санузел 2	6,29
	Итого по этажу	115,13

Условные обозначения

- ЩК — щит квартирный
- РК — распределительная коробка над дверью помещения
- магистраль от щита к РК: потолочное пространство, гофра
- мебель и сантехприборы — подложка

Допущения и предложения на листе

Основа листа: размеры и контуры этажей подобраны проектировщиком по составу помещений и площадям этажей с картинки 470 px (размеры на ней не читаются); обмер и исходный проект — задание (К-1); высоты: 1-й этаж 2800 мм, мансарда 2700 мм (горизонтальная часть) приняты; скаты кровли мансарды приняты по картинке: колено 1200 мм, уклон 45°, конёк вдоль длинной стороны; проект КР — задание (К-2); наружные стены 400 мм, перегородки 120 мм приняты (К-1); разрешённая мощность 15 кВт принята по типовым ТУ для частного дома (К-4); подрайон климата не задан — принят не северный (жилые от 2,5 м) (К-7).

Знак «*» — принято, не замерено и не подтверждено (замерить на объекте): К-2: отметка чистого пола этажа «Мансарда» +3,150 — принята без источника, все отметки мансарды считаются от неё; К-6: Л-1 — габарит марша снят с картинки заказчика (11 проступей в холле 3,6 м), а до отм. +3,150 нужно 18 подъёмов — одномаршевая не встаёт: решение по К-6.

См. лист открытых вопросов (лист 8, записи К-1, К-2, К-4, К-6, К-7).

Примечания

1. За отметку 0,000 принят уровень чистого пола. Высоты Н — от чистого пола до оси изделия; привязки — от чистовой грани стены до оси механизма (у рамки на несколько постов — до оси рамки).
2. Розеточные и мокрые линии — через УЗО или дифавтомат с током утечки не более 30 мА (ПУЭ 7.1.79); в санузле выполнить ДСУП (ПУЭ 7.1.87–7.1.88).
3. Кабель — медный, исполнение нг(А)-LS (ГОСТ 31565-2012); скрытая прокладка только горизонтально и вертикально, фактические трассы зафиксировать исполнительной схемой до закрытия отделкой.
4. Расчёт нагрузок, токов КЗ, селективности и сечений — по проекту ЭОМ организации с допуском СРО; лист задаёт состав, расположение и группы.
5. Щит квартиры (дома) — на 1-м этаже: кабели групп Мансарда поднимаются от щита в вертикальном кабель-канале (коробе) у лестницы и далее за потолком к точкам. Место короба и проход через перекрытие — задание конструктору; длины трасс этажа считаются после этого решения.

1000 мм · печать 1:1

Изм.	Кол.уч	Лист	№ док.	Подп.	Дата
Разраб.		Кырлан А.С.			04.11.26
Пров.					
ГИП					
Н. контр.					
Утв.					

ГД-2026-010-АИ

Дом 331 м²

Общая площадь 270,67* м² · * размеры приняты, не замерены (реестр — л. 8–10, К-1)

Дизайн-проект интерьера

Стадия	Лист	Листов
РП	49	216

План принципиальных трасс · Мансарда


М 1:75

Кырлан Александр Сергеевич

выпуск 04.11.2026 № 2a77323a49 · стр. 51 из 221

План слаботочных сетей · 1-й этаж

Интернет, ТВ, домофон · размеры в мм · высоты от чистого пола

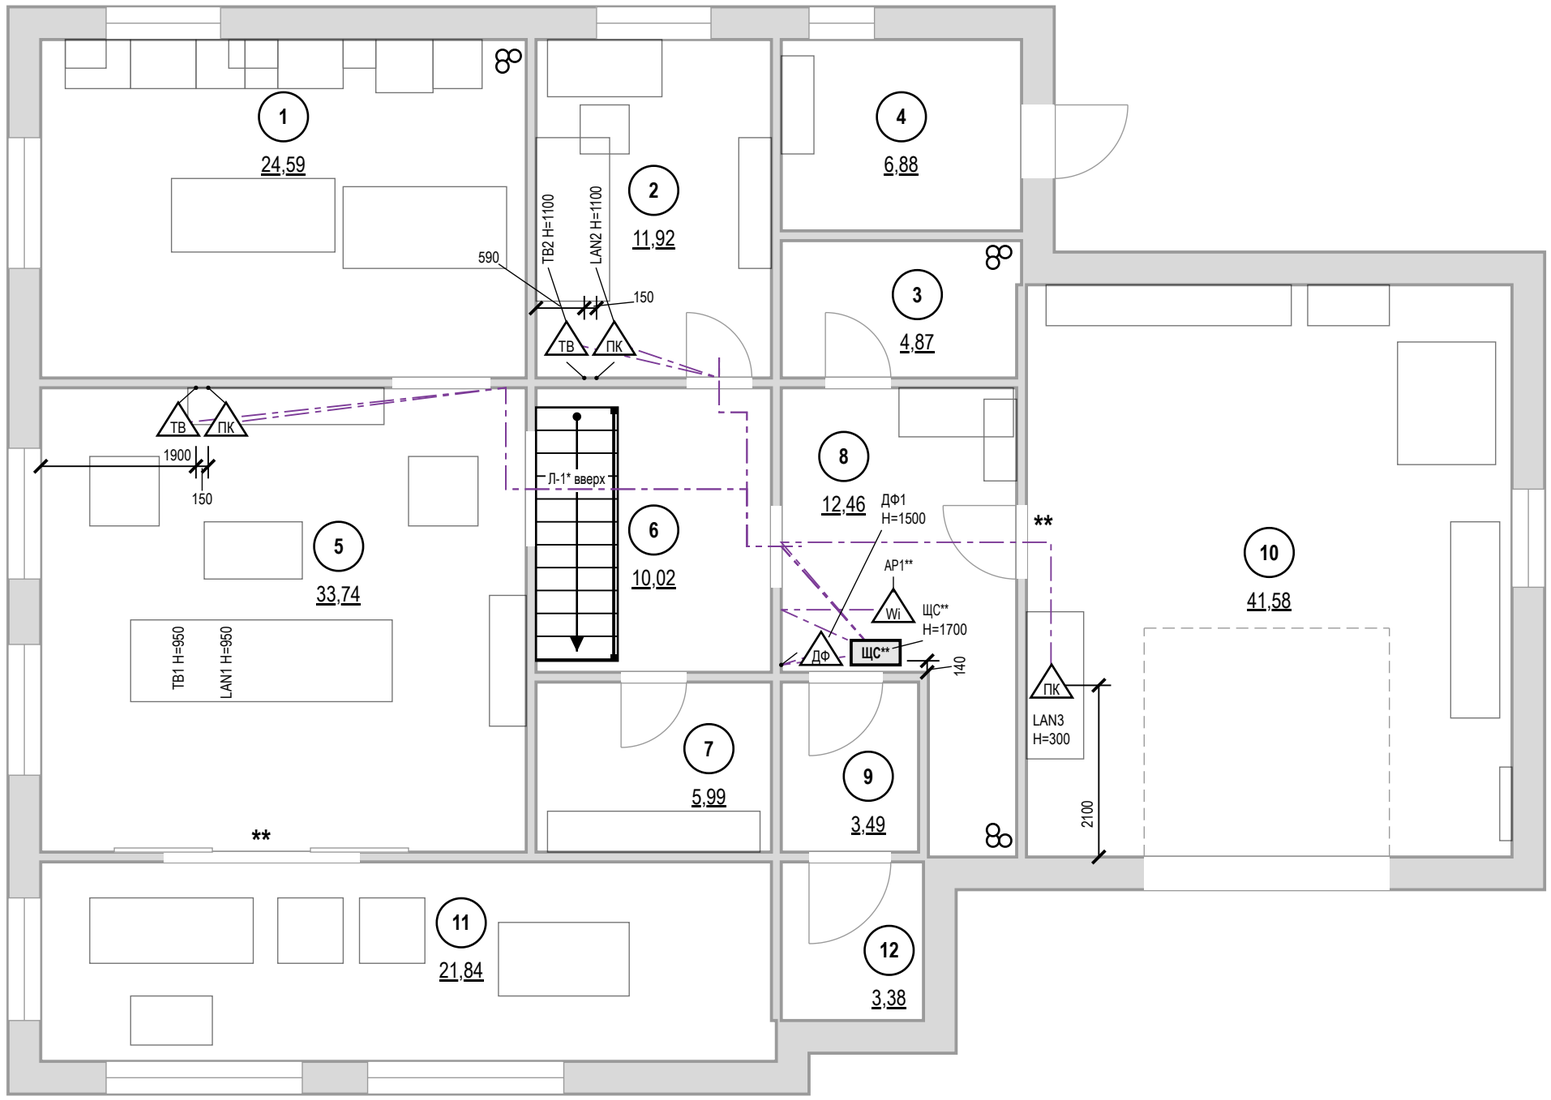

Ведомость слаботочных точек

Марка	Пом.	Назначение	H, мм	Кабель
ТВ2	2	розетка ТВ	1100	RG-6
LAN2	2	розетка LAN (RJ45)	1100	U/UTP кат. 6
ТВ1	5	розетка ТВ	950	коаксиальный RG-6
LAN1	5	розетка LAN (RJ45)	950	U/UTP кат. 6
ЩС**	8	щит слаботочный	1700	ввод пров.
ДФ1	8	домофон (трубка)	1500	по системе
АР1**	8	точка доступа Wi-Fi		U/UTP кат. 6
LAN3	10	розетка LAN (RJ45)	300	U/UTP кат. 5e/6

Условные обозначения

- ЩС — щит слаботочный: ввод провайдера, роутер, коммутатор
- ПК — розетка компьютерная RJ45
- ТВ — розетка телевизионная
- ДФ — трубка или монитор домофона
- Wi — точка доступа Wi-Fi (питание PoE)
- кабель от ЩС до точки, отдельным лучом
- мебель и сантехприборы — подложка
- стояк: К1 — канализация, В1 — ХВС, Т3 — ГВС
- 1 — номер помещения, площадь м²

Допущения и предложения на листе. Основа листа: размеры и контуры этажей подобраны проектировщиком по составу помещений и площадям этажей с картинки 470 px (размеры на ней не читаются); обмер и исходный проект — задание (К-1); высоты: 1-й этаж 2800 мм, мансарда 2700 мм (горизонтальная часть) приняты; скаты кровли мансарды приняты по картинке: колено 1200 мм, уклон 45°, конёк вдоль длинной стороны; проект КР — задание (К-2); наружные стены 400 мм, перегородки 120 мм приняты (К-1); разрешённая мощность 15 кВт принята по типовым ТУ для частного дома (К-4); подрайон климата не задан — принят не северный (жилые от 2,5 м) (К-7). Знак «*» — принято, не замерено и не подтверждено (замерить на объекте): К-6: Л-1 — габарит марша снят с картинки заказчика (11 проступей в холле 3,6 м), а до отм. +3,150 нужно 18 подъёмов — одномаршевая не встаёт: решение по К-6. Знак «**» — предложение проектировщика, заказчиком не утверждено (согласовать с заказчиком): ЩС — щит слаботочный: место и состав; АР1 — точка доступа Wi-Fi: число и места. См. лист открытых вопросов (лист 8, записи К-1, К-2, К-4, К-6, К-7; лист 9, запись К-9).

Примечания

1. За отметку 0,000 принят уровень чистого пола. Высоты H — от чистого пола до оси изделия; привязки — от чистовой грани стены до оси механизма (у рамки на несколько постов — до оси рамки).
2. Высота установки, не указанная на плане: розетки LAN и ТВ — 300 мм от чистого пола.
3. Слаботочные кабели — отдельно от силовых: в своей трубе или лотке, при параллельной прокладке не ближе 100 мм к силовым, пересечения под прямым углом; каждую точку — отдельным кабелем от ЩС** без скруток.
4. Трассы на листе — принципиальные; фактические зафиксировать исполнительной схемой до закрытия отделкой. Силовые линии, УЗО 30 мА, ДСУП, кабель нг(A)-LS — по листам розеток и щита.
5. Проект силовой части и расчёт токов КЗ — по проекту ЭОМ; слаботочная часть согласуется с провайдером (ввод в дом, место ONT) и с заказчиком (вызывная панель у калитки, антенна или спутниковое ТВ).

1000 мм · печать 1:1

Изм.	Кол.уч	Лист	№ док.	Подп.	Дата
Разраб.		Кырлан А.С.			04.11.26
Пров.					
ГИП					
Н. контр.					
Утв.					

ГД-2026-010-АИ

Дом 331 м²

Общая площадь 270,67* м² · * размеры приняты, не замерены (реестр — л. 8–10, К-1)

Дизайн-проект интерьера

Стадия	Лист	Листов
РП	50	216

План слаботочных сетей · 1-й этаж

М 1:75


Кырлан Александр Сергеевич

выпуск 04.11.2026 № 2a77323a49 · стр. 52 из 221

План слаботочных сетей · Мансарда

Интернет, ТВ, домофон · размеры в мм · высоты от чистого пола

ПРЕДВАРИТЕЛЬНО · не для производства работ · открыто пунктов: 15 (реестр — л. 8–10)

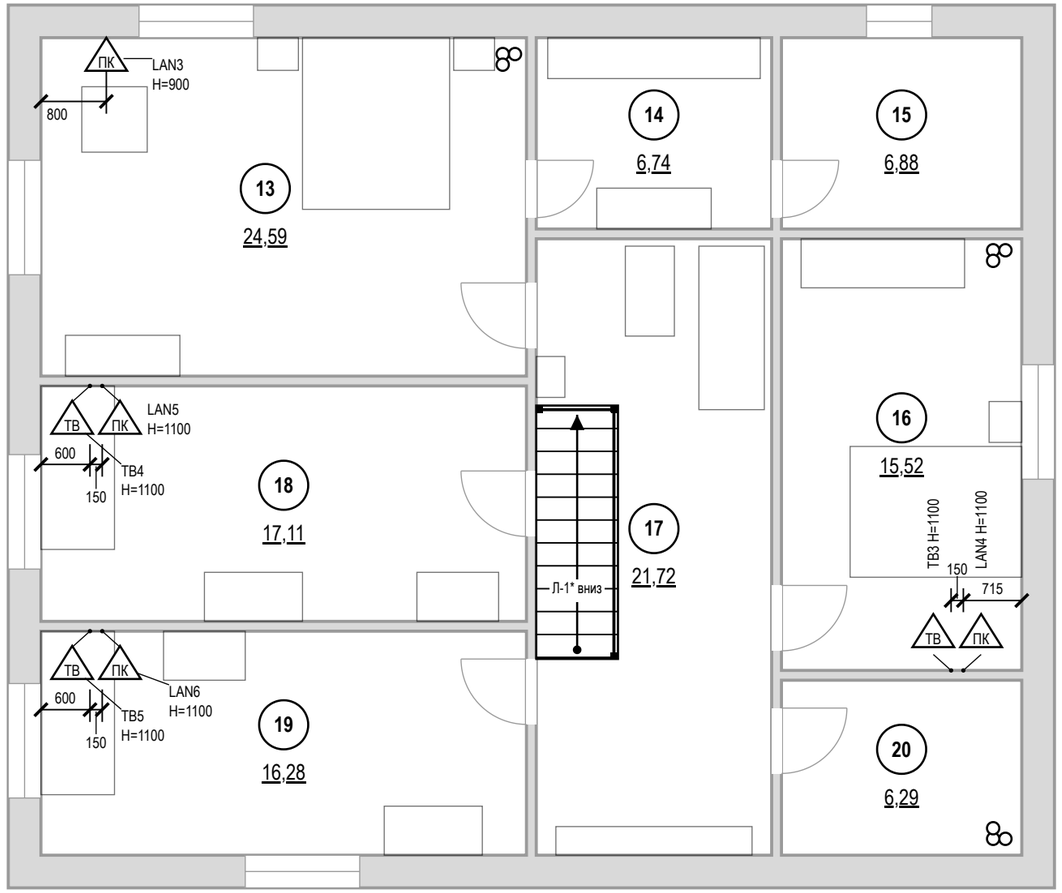

Ведомость слаботочных точек

Марка	Пом.	Назначение	H, мм	Кабель
LAN3	13	розетка LAN (RJ45)	900	U/UTP кат. 6
ТВ3	16	розетка ТВ	1100	RG-6
LAN4	16	розетка LAN (RJ45)	1100	U/UTP кат. 6
ТВ4	18	розетка ТВ	1100	RG-6
LAN5	18	розетка LAN (RJ45)	1100	U/UTP кат. 6
ТВ5	19	розетка ТВ	1100	RG-6
LAN6	19	розетка LAN (RJ45)	1100	U/UTP кат. 6

Условные обозначения

- ПК — розетка компьютерная RJ45
- ТВ — розетка телевизионная
- мебель и сантехприборы — подложка
- стояк: К1 — канализация, В1 — ХВС, Т3 — ГВС
- 1 — номер помещения, площадь м²

Допущения и предложения на листе

Основа листа: размеры и контуры этажей подобраны проектировщиком по составу помещений и площадям этажей с картинки 470 px (размеры на ней не читаются); обмер и исходный проект — задание (К-1); высоты: 1-й этаж 2800 мм, мансарда 2700 мм (горизонтальная часть) приняты; скаты кровли мансарды приняты по картинке: колено 1200 мм, уклон 45°, конёк вдоль длинной стороны; проект КР — задание (К-2); наружные стены 400 мм, перегородки 120 мм приняты (К-1); разрешённая мощность 15 кВт принята по типовым ТУ для частного дома (К-4); подрайон климата не задан — принят не северный (жилые от 2,5 м) (К-7).

Знак «*» — принято, не замерено и не подтверждено (замерить на объекте): К-2: отметка чистого пола этажа «Мансарда» +3,150 — принята без источника, все отметки мансарды считаются от неё; К-6: Л-1 — габарит марша снят с картинки заказчика (11 проступей в холле 3,6 м), а до отм. +3,150 нужно 18 подъёмов — одномаршевая не встаёт: решение по К-6.

Знак «**» — предложение проектировщика, заказчиком не утверждено (согласовать с заказчиком): ЩС — щит слаботочный: место и состав.

См. лист открытых вопросов (лист 8, записи К-1, К-2, К-4, К-6, К-7).

Примечания

1. За отметку 0,000 принят уровень чистого пола. Высоты H — от чистого пола до оси изделия; привязки — от чистовой грани стены до оси механизма (у рамки на несколько постов — до оси рамки).
2. Высота установки, не указанная на плане: розетки LAN и ТВ — 300 мм от чистого пола.
3. Слаботочные кабели — отдельно от силовых: в своей трубе или лотке, при параллельной прокладке не ближе 100 мм к силовым, пересечения под прямым углом; каждую точку — отдельным кабелем от ЩС** без скруток.
4. Трассы на листе — принципиальные; фактические зафиксировать исполнительной схемой до закрытия отделкой. Силовые линии, УЗО 30 мА, ДСУП, кабель нг(A)-LS — по листам розеток и щита.
5. Проект силовой части и расчёт токов КЗ — по проекту ЭОМ; слаботочная часть согласуется с провайдером (ввод в дом, место ONT) и с заказчиком (вызывная панель у калитки, антенна или спутниковое ТВ).

1000 мм · печать 1:1

Изм.	Кол.уч	Лист	№ док.	Подп.	Дата
Разраб.		Кырлан А.С.			04.11.26
Пров.					
ГИП					
Н. контр.					
Утв.					

ГД-2026-010-АИ

Дом 331 м²

Общая площадь 270,67* м² · * размеры приняты, не замерены (реестр — л. 8–10, К-1)

Дизайн-проект интерьера

Стадия	Лист	Листов
РП	51	216

План слаботочных сетей · Мансарда

М 1:75

Кырлан Александр Сергеевич


выпуск 04.11.2026 № 2a77323a49 · стр. 53 из 221

План вентиляции · 1-й этаж

Вытяжка, приток, переток · кондиционирование не предусмотрено · размеры в мм · высоты от чистого пола

ПРЕДВАРИТЕЛЬНО · не для производства работ · открыто пунктов: 15 (реестр — л. 8–10)

Допущения и предложения на листе. Основа листа: размеры и контуры этажей подобраны проектировщиком по составу помещений и площадям этажей с картинки 470 px (размеры на ней не читаются); обмер и исходный проект — задание (К-1); высоты: 1-й этаж 2800 мм, мансарда 2700 мм (горизонтальная часть) приняты; скаты кровли мансарды приняты по картинке: колено 1200 мм, уклон 45°, конёк вдоль длинной стороны; проект КР — задание (К-2); наружные стены 400 мм, перегородки 120 мм приняты (К-1); разрешённая мощность 15 кВт принята по типовым ТУ для частного дома (К-4); подрайон климата не задан — принят не северный (жилые от 2,5 м) (К-7). Знак «*» — принято, не замерено (замерить): К-6: Л-1. Знак «**» — предложено, не утверждено (согласовать). См. лист открытых вопросов (лист 8, записи К-1, К-2, К-4, К-6, К-7; лист 9, записи К-9, К-11, К-12).

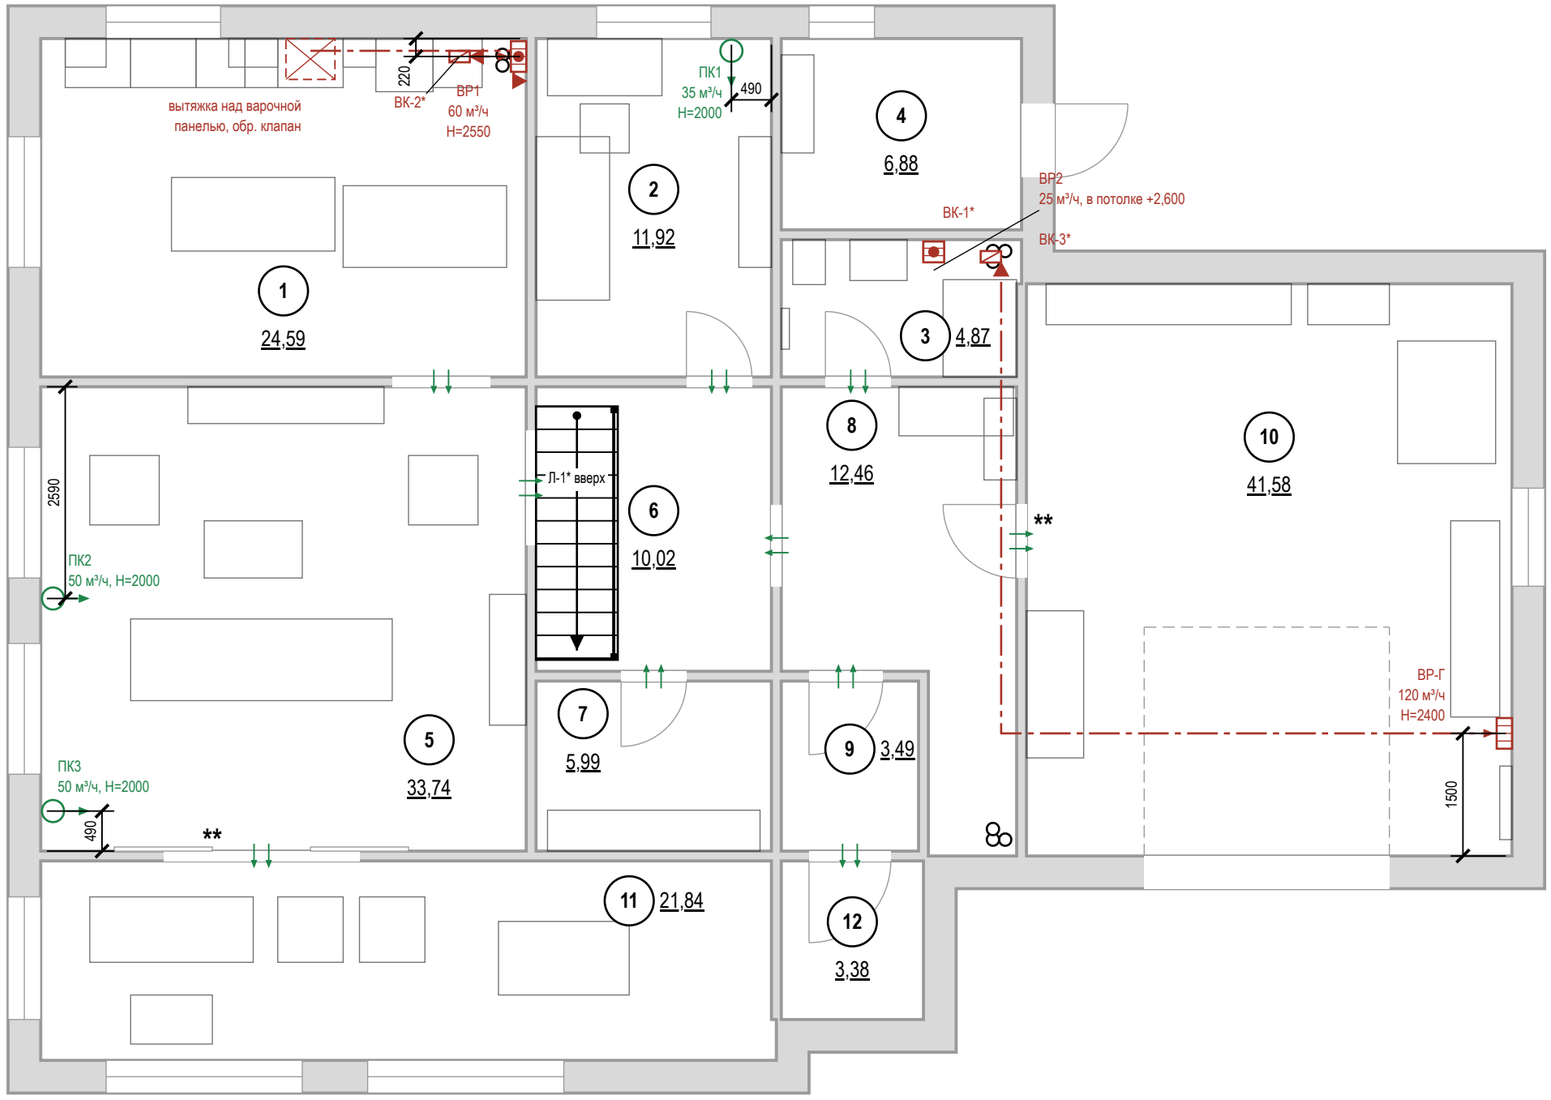

Условные обозначения

- стояк: К1 — канализация, В1 — ХВС, Т3 — ГВС
- 1 — номер помещения, площадь м²
- вытяжная решётка в вентканал: марка, расход м³/ч, H центра от чистого пола
- вытяжная решётка с бытовым вентилятором и обратным клапаном: марка, расход, H
- вентилятор с обратным клапаном в подшивном потолке, воздуховод за потолком до канала
- приточный клапан (КИВ) в наружной стене: марка, расход, H центра
- переток: зазор под полотном или переточная решётка
- кухонная вытяжка над варочной панелью
- вентканал ВК-N; «*» — принят до обмера
- воздуховод в коробе под потолком (за подшивным потолком) до вентканала
- отдельный вход воздуховода в вентканал, обратный клапан
- ** — «**» — предложение проектировщика, заказчиком не утверждено

Воздухообмен, м³/ч

№	Помещение	Выт. норма	Выт. проект	Прит. норма	Прит. проект	Устрой-ства
1	Кухня-столовая	60	60			ВР1
2	Кабинет-гостевая			34	35	ПК1
3	Санузел 1 этажа	25	25			ВР2
4	Котельная	4				наружу, см. прим.
5	Гостиная			95	100	ПК2, ПК3
7	Кладовая	3				переток
10	Гараж	23	120			ВР-Г
	Итого	**115**	**205**	**129**	**135**	

Воздухообмен этажа — по большей из сумм притока и вытяжки: норма 129 м³/ч, проект 205 м³/ч.
Вытяжка не меньше притока — баланс сведён.

Привязки — до обмера
Вентканалы ВК-N* приняты проектировщиком, решётки и воздуховоды — от них. До черновых работ — обмер каналов и тяги, лист перевыпустить по факту.

Примечания

1. Расчёт систем ОВ и подбор оборудования — проектная организация с допуском СРО; лист даёт места, трассы и привязки.
2. Нормы одноквартирного дома — СП 55.13330.2016, п. 9.7: в жилых комнатах не менее однократного воздухообмена в час, из кухни не менее 60 м³/ч, из ванной, туалета, совмещённого санузла не менее 25 м³/ч; кухня с газовой плитой — 100 м³/ч в запас. Системы — по СП 60.13330.2020.
3. Вентканалы и шахты не сужать, не переносить и не закрывать; вентилятор и кухонная вытяжка — через обратный клапан, без перекрытия естественной тяги; ВР1 — воздуховодом до ВК-2 ≈ 0,7 м, ВР-Г — воздуховодом до ВК-3 ≈ 12,0 м (нужен вентилятор) в коробе под потолком.
4. Проектные расходы — не ниже нормы, вытяжка сведена с притоком вентиляторами мокрых помещений. Клапаны — в простенке у окна, центр 2000 мм, не над кроватью, не ближе 300 мм к стоякам отопления; типоразмер — на расход.
5. Под подшивным потолком вытяжка — в потолке, воздуховодом за потолком до канала. Кухонная вытяжка в воздухообмен не включена: воздуховод не менее Ø125 в коробе, вход в канал отдельный.
6. Переток — зазор под полотнами межкомнатных дверей или переточная решётка.
7. Котельная (пом. 4), Гараж (пом. 10) — вытяжка наружу своим каналом, воздух в жилую часть не перетекает (выхлоп, продукты сгорания); приток — с улицы. Воздухообмен котельной — по паспорту котла и СП 60.13330.2020, при газовом котле — СП 62.13330; тип котла не выбран — устройства не показаны до решения.
8. Кондиционирование заданием не предусмотрено; при установке трассы фреона и дренажа (не менее 40 мм/м, в К1 через сифон) и питание заложить до черновых работ.
9. Привязки оборудования — по паспортам приобретённых моделей, до черновых работ.

1000 мм · печать 1:1

Изм.	Кол.уч	Лист	№ док.	Подп.	Дата
Разраб.		Кырлан А.С.			04.11.26
Пров.					
ГИП					
Н. контр.					
Утв.					

ГД-2026-010-АИ

Дом 331 м²

Общая площадь 270,67* м² · * размеры приняты, не замерены (реестр — л. 8–10, К-1)

Дизайн-проект интерьера

Стадия	Лист	Листов
РП	52	216

План вентиляции · 1-й этаж


М 1:75

Кырлан Александр Сергеевич

выпуск 04.11.2026 № 2a77323a49 · стр. 54 из 221

План вентиляции · Мансарда

Вытяжка, приток, переток · кондиционирование не предусмотрено · размеры в мм · высоты от чистого пола

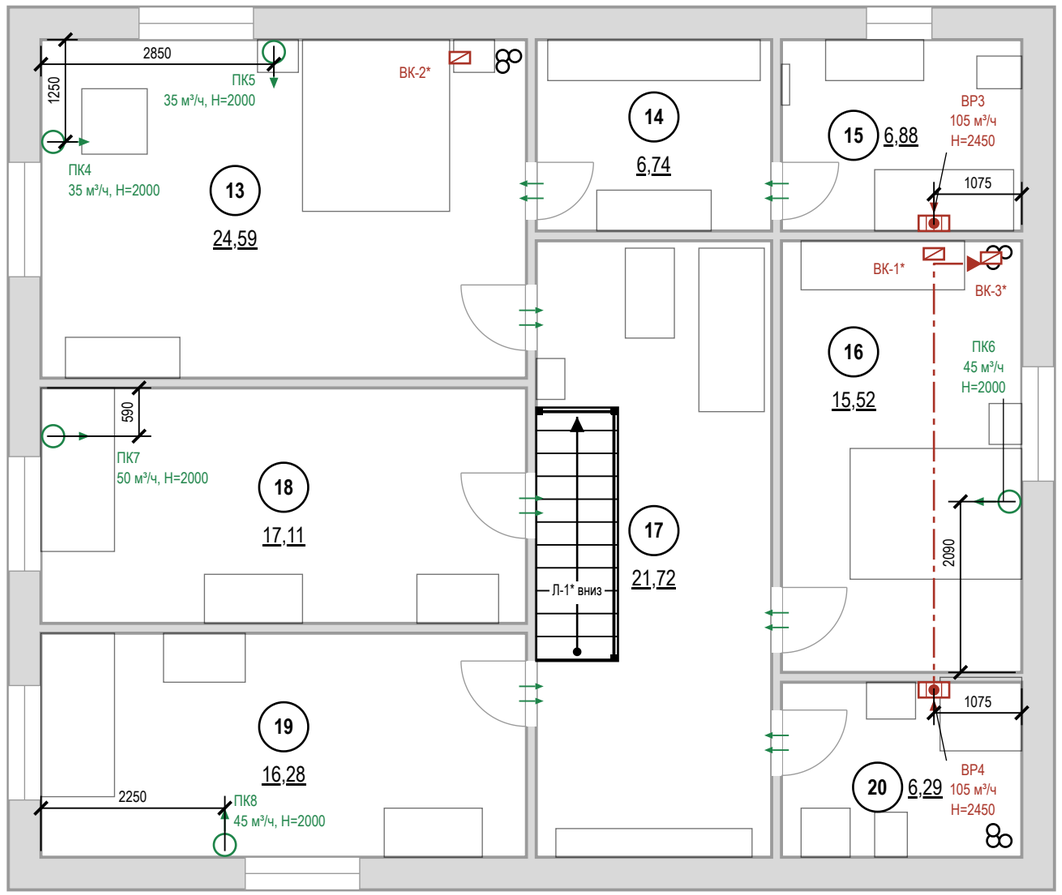

Условные обозначения

- стояк: К1 — канализация, В1 — ХВС, Т3 — ГВС
- (1) номер помещения, площадь м²
- вытяжная решётка с бытовым вентилятором и обратным клапаном: марка, расход, Н
- приточный клапан (КИВ) в наружной стене: марка, расход, Н центра
- переток: зазор под полотном или переточная решётка
- вентканал ВК-N; «*» — принят до обмера
- воздуховод в коробе под потолком (за подшивным потолком) до вентканала
- отдельный вход воздуховода в вентканал, обратный клапан

Воздухообмен, м³/ч

№	Помещение	Выт. норма	Выт. проект	Прит. норма	Прит. проект	Устрой-ства
13	Спальня мастер			67	70	ПК4, ПК5
14	Гардеробная мастер	4				переток
15	Санузел мастер	25	105			ВР3
16	Спальня 2			42	45	ПК6
18	Спальня 3			47	50	ПК7
19	Спальня 4			44	45	ПК8
20	Санузел 2	25	105			ВР4
	Итого	**54**	**210**	**200**	**210**	

Воздухообмен этажа — по большей из сумм притока и вытяжки: норма 200 м³/ч, проект 210 м³/ч.
Вытяжка не меньше притока — баланс сведён.

Привязки — до обмера
Вентканалы ВК-N* приняты проектировщиком, решётки и воздуховоды — от них. До черновых работ — обмер каналов и тяги, лист перевыпустить по факту.

Допущения и предложения на листе
Основа листа: размеры и контуры этажей подобраны проектировщиком по составу помещений и площадям этажей с картинки 470 px (размеры на ней не читаются); обмер и исходный проект — задание (К-1); высоты: 1-й этаж 2800 мм, мансарда 2700 мм (горизонтальная часть) приняты; скаты кровли мансарды приняты по картинке: колено 1200 мм, уклон 45°, конёк вдоль длинной стороны; проект КР — задание (К-2); наружные стены 400 мм, перегородки 120 мм приняты (К-1); разрешённая мощность 15 кВт принята по типовым ТУ для частного дома (К-4); подрайон климата не задан — принят не северный (жилые от 2,5 м) (К-7).
Знак «*» — принято, не замерено и не подтверждено (замерить на объекте): К-2: отметка чистого пола этажа «Мансарда» +3,150 — принята без источника, все отметки мансарды считаются от неё; К-6: Л-1 — габарит марша снят с картинки заказчика (11 проступей в холле 3,6 м), а до отм. +3,150 нужно 18 подъёмов — одномаршевая не встаёт: решение по К-6.
Открытые вопросы и конфликты по листу: К-11, К-12.
См. лист открытых вопросов (лист 8, записи К-1, К-2, К-4, К-6, К-7; лист 9, записи К-11, К-12).

Примечания

1. Расчёт систем ОВ и подбор оборудования — проектная организация с допуском СРО; лист даёт места, трассы и привязки.
2. Нормы однокварти рного дома — СП 55.13330.2016, п. 9.7: в жилых комнатах не менее однократного воздухообмена в час, из кухни не менее 60 м³/ч, из ванной, туалета, совмещённого санузла не менее 25 м³/ч; кухня с газовой плитой — 100 м³/ч в запас. Системы — по СП 60.13330.2020.
3. Вентканалы и шахты не сужать, не переносить и не закрывать; вентилятор и кухонная вытяжка — через обратный клапан, без перекрытия естественной тяги; ВР4 — воздуховодом до ВК-3 ≈ 6,0 м в коробе под потолком.
4. Проектные расходы — не ниже нормы, вытяжка сведена с притоком вентиляторами мокрых помещений. Клапаны — в простенке у окна, центр 2000 мм, не над кроватью, не ближе 300 мм к стоякам отопления; типоразмер — на расход.
5. Переток — зазор под полотнами межкомнатных дверей или переточная решётка.
6. Кондиционирование заданием не предусмотрено; при установке трассы фреона и дренажа (не менее 40 мм/м, в К1 через сифон) и питание заложить до черновых работ.
7. Привязки оборудования — по паспортам приобретённых моделей, до черновых работ.

1000 мм · печать 1:1

Изм.	Кол.уч	Лист	№ док.	Подп.	Дата
Разраб.		Кырлан А.С.			04.11.26
Пров.					
ГИП					
Н. контр.					
Утв.					

ГД-2026-010-АИ

Дом 331 м²

Общая площадь 270,67* м² · * размеры приняты, не замерены (реестр — л. 8–10, К-1)

Дизайн-проект интерьера

Стадия	Лист	Листов
РП	53	216

План вентиляции · Мансарда

М 1:75


Кырлан Александр Сергеевич

выпуск 04.11.2026 № 2a77323a49 · стр. 55 из 221

План отопления · 1-й этаж

Радиаторы, стояки, подводки · размеры в мм · высоты от чистого пола

ПРЕДВАРИТЕЛЬНО · не для производства работ · открыто пунктов: 15 (реестр — л. 8–10)

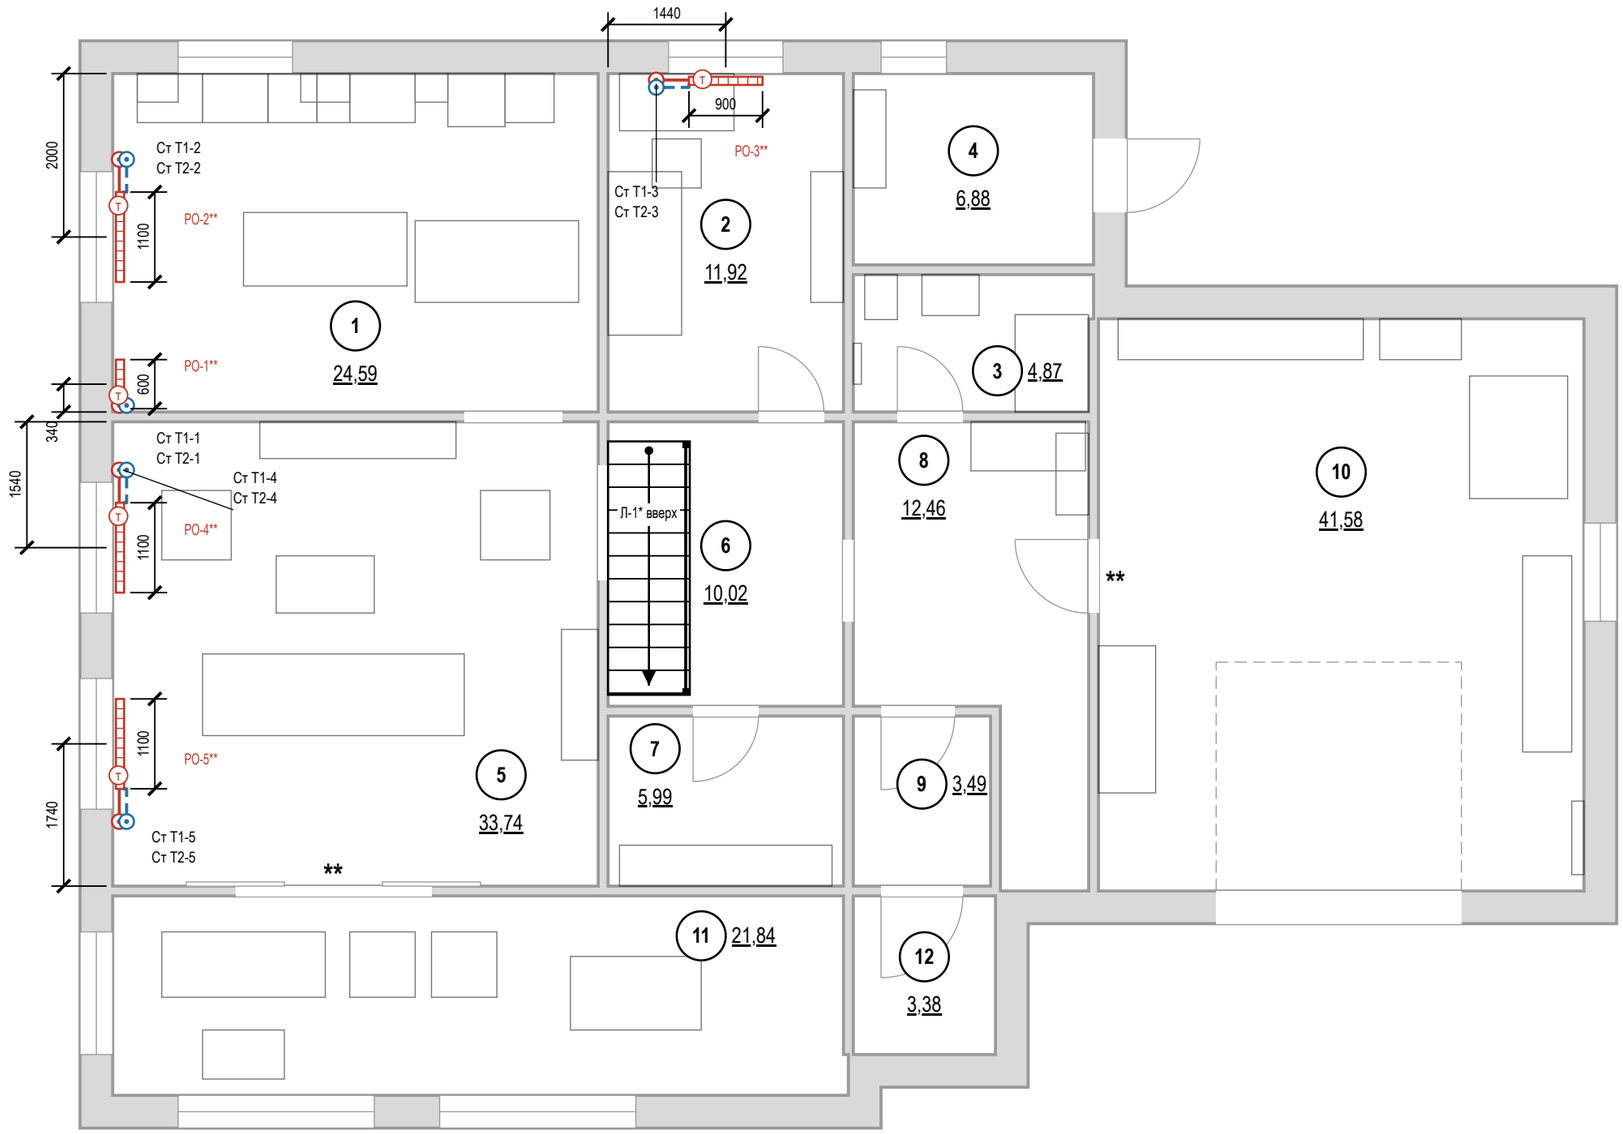

Условные обозначения

- (1) — номер помещения, площадь м²
- радиатор отопления (марка РО-N, длина по плану)
- клапан с термоголовкой на подаче
- стояк отопления, подающий (Ст Т1-N)
- стояк отопления, обратный (Ст Т2-N)
- Т1 — отопление, подающий трубопровод
- Т2 — отопление, обратный трубопровод
- ** — «**» — предложение проектировщика, заказчиком не утверждено

Ведомость радиаторов

Марка	Помещение	Тип	Д×В×Г, мм	Низ / стена	Q, Вт
РО-1**	1. Кухня-столовая		600×600×100	120 / 40	расч.
РО-2**	1. Кухня-столовая		1100×600×100	120 / 40	расч.
РО-3**	2. Кабинет-гостевая		900×600×100	120 / 40	расч.
РО-4**	5. Гостиная		1100×600×100	120 / 40	расч.
РО-5**	5. Гостиная		1100×600×100	120 / 40	расч.

Низ — от чистого пола, стена — зазор до задней панели, мм.

Привязки — до обмера

Подъёмы подводок отопления в исходных данных не заданы: показаны у откосов окон и у торцов приборов принципиально, разводка — от котла (котельная, пом. 4) через распределительный коллектор. До черновых работ — место котла, коллектора и подъёмов труб и паспорта приборов; лист перевыпустить по факту.

Допущения и предложения на листе. Основа листа: размеры и контуры этажей подобраны проектировщиком по составу помещений и площадям этажей с картинки 470 px (размеры на ней не читаются); обмер и исходный проект — задание (К-1); высоты: 1-й этаж 2800 мм, мансарда 2700 мм (горизонтальная часть) приняты; скаты кровли мансарды приняты по картинке: колено 1200 мм, уклон 45°, конёк вдоль длинной стороны; проект КР — задание (К-2); наружные стены 400 мм, перегородки 120 мм приняты (К-1); разрешённая мощность 15 кВт принята по типовым ТУ для частного дома (К-4); подрайон климата не задан — принят не северный (жилые от 2,5 м) (К-7). Знак «*» — принято, не замерено (замерить): К-6: Л-1. Знак «**» — предложено, не утверждено (согласовать): ИЗ-2, К-11, Кф-1: РО-1; К-11: РО-2, РО-3, РО-4, РО-5. См. лист открытых вопросов (лист 8, записи К-1, К-2, К-4, К-6, К-7; лист 9, записи К-9, К-11; лист 10, записи ИЗ-2, Кф-1).

Примечания

1. Расчёт системы отопления, теплопотерь и подбор приборов — проектная организация с допуском СРО; лист даёт места и привязки.
2. Тип, длина и мощность радиаторов — по теплотехническому расчёту; лист задаёт места, зазоры и подключение.
3. Зазоры радиатора: низ не менее 100 мм от чистого пола, верх не менее 100 мм до подоконника, 30–50 мм от стены до задней панели; центр по оси окна с допуском ±20 мм. Верх до подоконника — 180 мм. Радиаторы не закрывать глухими коробами и мебелью; трубы через стены и перекрытия в гильзах.
4. Источник тепла — котёл в котельной (пом. 4): тип (газ / электро / твёрдое топливо) и мощность — по решению заказчика и расчёту (СП 60.13330.2020); до выбора разводка от коллектора принципиальная.
5. Без отопительного прибора: пом. 3, пом. 6, пом. 7 — внутренние, без наружных стен, окон и дверей наружу, обогреваются от смежных помещений; полотенцесушитель — по листам ВК.
6. Прибор не задан: пом. 8 (дверь наружу), 9 (дверь наружу) — прибор (у входной двери — конвектор) или тёплый пол по расчёту до черновых работ.
7. Привязки приборов и подводок — по паспортам приобретённых радиаторов и клапанов, до черновых работ.
8. До закрытия отделкой трубопроводы отопления испытать гидростатическим давлением с оформлением акта (СП 73.13330.2016, 7.2–7.3).

1000 мм · печать 1:1

Изм.	Кол.уч	Лист	№ док.	Подп.	Дата
Разраб.		Кырлан А.С.			04.11.26
Пров.					
ГИП					
Н. контр.					
Утв.					

ГД-2026-010-АИ

Дом 331 м²

Общая площадь 270,67* м² · * размеры приняты, не замерены (реестр — л. 8–10, К-1)

Дизайн-проект интерьера

Стадия	Лист	Листов
РП	54	216

План отопления · 1-й этаж


М 1:75

Кырлан Александр Сергеевич

выпуск 04.11.2026 № 2a77323a49 · стр. 56 из 221

План отопления · Мансарда

Радиаторы, стояки, подводки · размеры в мм · высоты от чистого пола

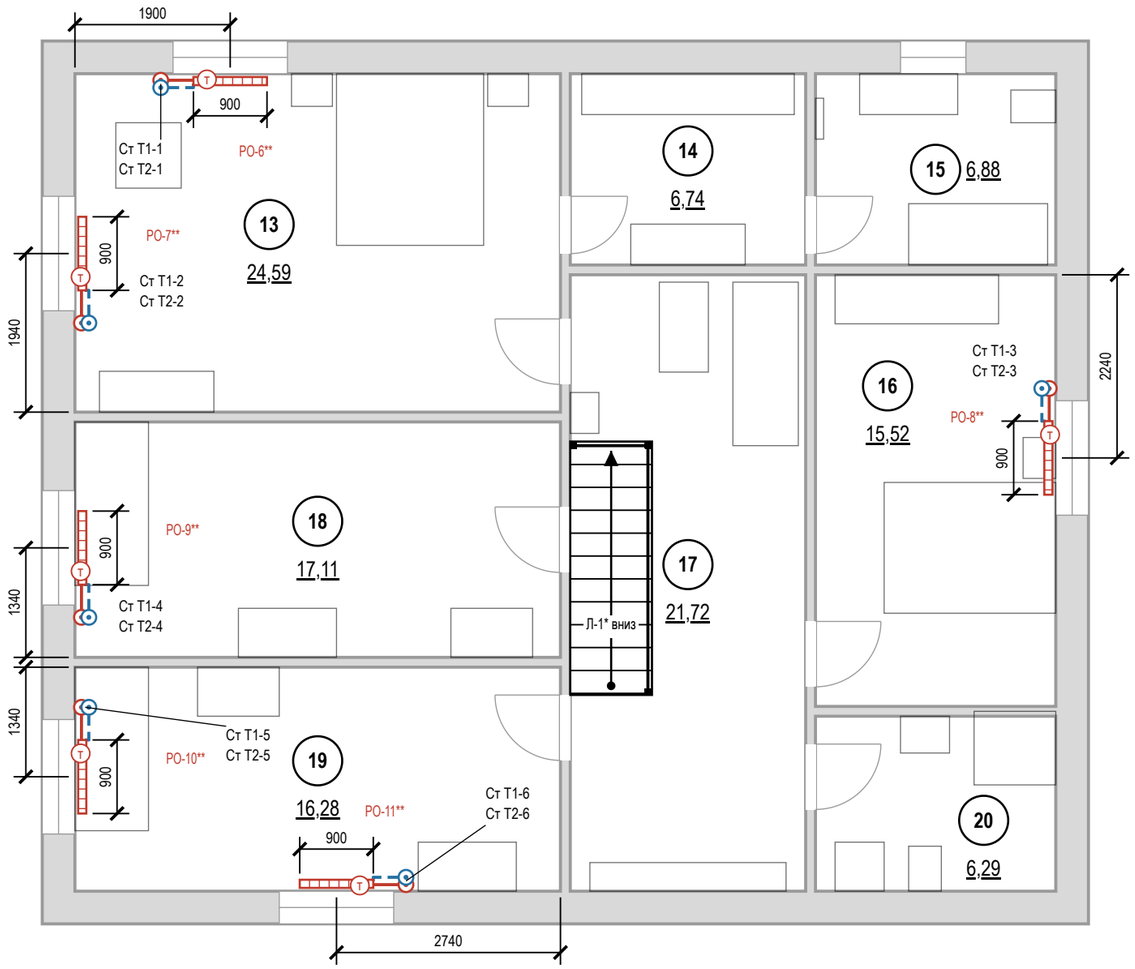

Условные обозначения

- (1) — номер помещения, площадь м²
- радиатор отопления (марка РО-N, длина по плану)
- (Т) — клапан с термоголовкой на подаче
- стояк отопления, подающий (Ст Т1-N)
- стояк отопления, обратный (Ст Т2-N)
- Т1 — отопление, подающий трубопровод
- Т2 — отопление, обратный трубопровод

Ведомость радиаторов

Марка	Помещение	Тип	Д×В×Г, мм	Низ / стена	Q, Вт
РО-6**	13. Спальня мастер		900×600×100	120 / 40	расч.
РО-7**	13. Спальня мастер		900×600×100	120 / 40	расч.
РО-8**	16. Спальня 2		900×600×100	120 / 40	расч.
РО-9**	18. Спальня 3		900×600×100	120 / 40	расч.
РО-10**	19. Спальня 4		900×600×100	120 / 40	расч.
РО-11**	19. Спальня 4		900×600×100	120 / 40	расч.

Низ — от чистого пола, стена — зазор до задней панели, мм.

Привязки — до обмера

Подъёмы подводок отопления в исходных данных не заданы: показаны у откосов окон принципиально, разводка — от котла (котельная, пом. 4) через распределительный коллектор. До черновых работ — место котла, коллектора и подъёмов труб и паспорта приборов; лист перевыпустить по факту.

Примечания

1. Расчёт системы отопления, теплопотерь и подбор приборов — проектная организация с допуском СРО; лист даёт места и привязки.
2. Тип, длина и мощность радиаторов — по теплотехническому расчёту; лист задаёт места, зазоры и подключение.
3. Зазоры радиатора: низ не менее 100 мм от чистого пола, верх не менее 100 мм до подоконника, 30–50 мм от стены до задней панели; центр по оси окна с допуском ±20 мм. Верх до подоконника — 180 мм. Радиаторы не закрывать глухими коробами и мебелью; трубы через стены и перекрытия в гильзах.
4. Источник тепла — котёл в котельной (пом. 4): тип (газ / электро / твёрдое топливо) и мощность — по решению заказчика и расчёту (СП 60.13330.2020); до выбора разводка от коллектора принципиальная.
5. Прибор не задан: пом. 15, 17, 20 — прибор или тёплый пол по расчёту до черновых работ.
6. Привязки приборов и подводок — по паспортам приобретённых радиаторов и клапанов, до черновых работ.
7. До закрытия отделкой трубопроводы отопления испытать гидростатическим давлением с оформлением акта (СП 73.13330.2016, 7.2–7.3).

Допущения и предложения на листе. Основа листа: размеры и контуры этажей подобраны проектировщиком по составу помещений и площадям этажей с картинки 470 px (размеры на ней не читаются); обмер и исходный проект — задание (К-1); высоты: 1-й этаж 2800 мм, мансарда 2700 мм (горизонтальная часть) приняты; скаты кровли мансарды приняты по картинке: колено 1200 мм, уклон 45°, конёк вдоль длинной стороны; проект КР — задание (К-2); наружные стены 400 мм, перегородки 120 мм приняты (К-1); разрешённая мощность 15 кВт принята по типовым ТУ для частного дома (К-4); подрайон климата не задан — принят не северный (жилые от 2,5 м) (К-7). Знак «*» — принято, не замерено и не подтверждено (замерить на объекте): К-2: отметка чистого пола этажа «Мансарда» +3,150 — принята без источника, все отметки мансарды считаются от неё; К-6: Л-1 — габарит марша снят с картинки заказчика (11 проступей в холле 3,6 м), а до отм. +3,150 нужно 18 подъёмов — одномаршевая не встаёт: решение по К-6. Знак «**» — предложение проектировщика, заказчиком не утверждено (согласовать с заказчиком): К-11: РО-6, РО-7, РО-8, РО-9, РО-10, РО-11 — прибор под окном по оси проёма, ширина ≈ 0,7 ширины окна — предложение ОВ (лист ОВ выводил его сам до, теперь он в данных — один источник для листа, мебели, DXF и IFC); котёл и мощность не выбраны (К-11) — размер по теплотехническому расчёту. См. лист открытых вопросов (лист 8, записи К-1, К-2, К-4, К-6, К-7; лист 9, запись К-11; лист 10, записи ИЗ-2, Кф-1); по листу — К-11, Кф-1, ИЗ-2.

1000 мм · печать 1:1

Изм.	Кол.уч	Лист	№ док.	Подп.	Дата
Разраб.		Кырлан А.С.			04.11.26
Пров.					
ГИП					
Н. контр.					
Утв.					

ГД-2026-010-АИ

Дом 331 м²

Общая площадь 270,67* м² · * размеры приняты, не замерены (реестр — л. 8–10, К-1)

Дизайн-проект интерьера

Стадия	Лист	Листов
РП	55	216

План отопления · Мансарда

М 1:75

Кырлан Александр Сергеевич


выпуск 04.11.2026 № 2a77323a49 · стр. 57 из 221

План выводов сантехники · 1-й этаж


Выводы В1, Т3, К1 · привязки от чистовых стен · высоты от чистого пола, мм

ПРЕДВАРИТЕЛЬНО · не для производства работ · открыто пунктов: 15 (реестр — л. 8–10)

Фрагмент 1. Санузел 1 этажа (пом. 3)

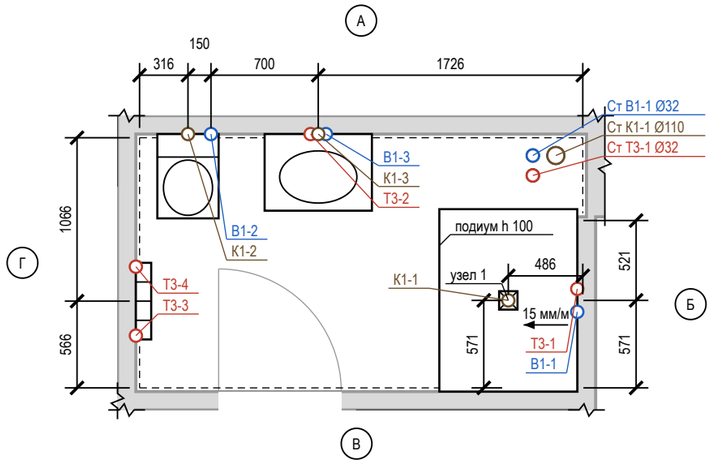

Фрагмент 2. Кухня-столовая (пом. 1)

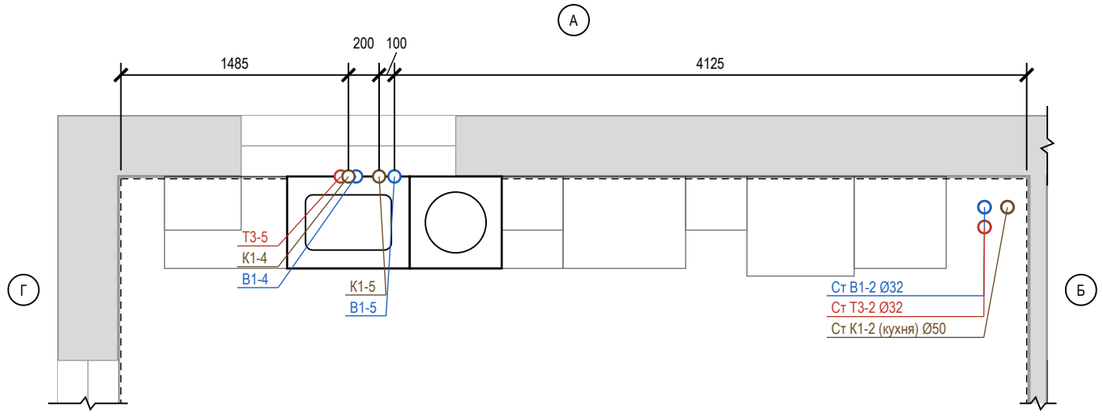

Ведомость привязок выводов

Код	Прибор	Ø	H, мм	Привязка от чист. стен, мм	Прим.
В1-1	Сн1** душ	½"	1300*	ст. Б: 496 от В	межос. 150; 1200* от пола душа (подиум 100, +0,085)
Т3-1	Сн1** душ	½"	1300*	ст. Б: 446 от В	межос. 150; 1200* от пола душа (подиум 100, +0,085)
К1-1	Сн1** душ	Ø50	100	486 от Б; 571 от В	трап в подиуме 100
В1-2	Сн2 унитаз подвесной	½"	250*	ст. А: 466 от Г	в раме инсталляции
К1-2	Сн2 унитаз подвесной	Ø110	220*	ст. А: 316 от Г	
В1-3	Сн3 умывальник	½"	600*	ст. А: 1216 от Г	межос. 100
Т3-2	Сн3 умывальник	½"	600*	ст. А: 1116 от Г	межос. 100
К1-3	Сн3 умывальник	Ø50	500*	ст. А: 1166 от Г	
Т3-3	Сн4 полотенцесушитель	½"	1150*	ст. Г: 341 от В	подача, межос. 450; байпас и краны
Т3-4	Сн4 полотенцесушитель	½"	1150*	ст. Г: 791 от В	обратка
В1-4	Кх1 мойка кухонная	½"	600*	ст. А: 1535 от Г	межос. 100
Т3-5	Кх1 мойка кухонная	½"	600*	ст. А: 1435 от Г	межос. 100
К1-4	Кх1 мойка кухонная	Ø50	400*	ст. А: 1485 от Г	
В1-5	Кх2 посудомоечная машина	½"	550*	ст. А: 1785 от Г	кран ПММ в шкафу мойки
К1-5	Кх2 посудомоечная машина	Ø40	550*	ст. А: 1685 от Г	слив ПММ в шкафу мойки

* — высота по практике монтажа; сверить по паспорту прибора

Условные обозначения

- вывод В1 (код — в ведомости привязок)
- вывод Т3 (код — в ведомости привязок)
- вывод К1 (код — в ведомости привязок)
- сантехприбор по расстановке (габарит модели)
- чистовая поверхность стены (от неё привязки)
- стояк «Ст К1-N / Ст В1-N» (ГОСТ 21.601), Ø мм
- линия обрыва (граница фрагмента)
- трап / лоток в полу
- направление уклона К1 / пола: Ø, мм на 1 м
- обозначение стены А–Г (как на развёртках)

Допущения и предложения на листе. Основа листа: размеры и контуры этажей подобраны проектировщиком по составу помещений и площадям этажей с картинки 470 px (размеры на ней не читаются); обмер и исходный проект — задание (К-1); высоты: 1-й этаж 2800 мм, мансарда 2700 мм (горизонтальная часть) приняты; скаты кровли мансарды приняты по картинке: колено 1200 мм, уклон 45°, конёк вдоль длинной стороны; проект КР — задание (К-2); наружные стены 400 мм, перегородки 120 мм приняты (К-1); разрешённая мощность 15 кВт принята по типовым ТУ для частного дома (К-4); подрайон климата не задан — принят не северный (жилые от 2,5 м) (К-7). Знак «**» — предложение проектировщика, заказчиком не утверждено (согласовать с заказчиком): К-8: Сн1 — Подиум душевой зоны 100 мм — предложение проектировщика: трап в стяжке 35 мм не встаёт (монтажная высота трапа 90 + уклон отвода до стояка 42 = 132 мм). См. лист открытых вопросов (лист 8, записи К-1, К-2, К-4, К-7; лист 9, запись К-8); по листу — К-8.

Примечания

1. Привязки выводов даны от чистовых поверхностей стен (облицовка на сторону: санузел 1 этажа — 24 мм (штукатурка 10 + клей 5 + плитка 9); кухня-столовая — 22 мм (фартук: штукатурка 10 + клей 3 + плитка 9)); эти же грани — на развёртках и в раскладке плитки. Высоты — от чистого пола помещения.
2. Высоты и межосевые, отмеченные «*», приняты по практике монтажа; до черновой разводки сверить по паспорту выбранного прибора (смеситель, инсталляция, сифон).
3. Горячая вода (Т3) — слева от холодной (В1), если смотреть на прибор. Допуск установки выводов: ±5 мм в группе, ±20 мм у отдельно стоящих.
4. Расчёт систем водоснабжения и канализации и подбор оборудования выполняет проектная организация; лист задаёт места и высоты выводов.
5. Сн1** душ (В1-1, Т3-1, К1-1): трап в подиуме 100 мм — верх подиума у решётки трапа +0,085, к краю поднимается уклоном 15 мм/м: ступень по открытому краю 109 мм (край показан на плане); «узел 1» — на схеме разводки; подиум — предложение, согласовать с заказчиком. Водорозетки В1-1, Т3-1 — 1200 мм от пола душа, то есть 1300 мм от чистого пола помещения: стену размечают до подиума.
6. Посудомоечная машина Кх2: кран и слив — отдельными выводами в шкафу мойки (не за машиной), до машины ≤ 1500 мм.
7. Прибор Кх1 мойка кухонная, Кх2 посудомоечная машина взят из расстановки мебели (по шкафу с мойкой).
8. Стояки в коробах/шахтах не замоноличивать; стояк К1 в коробе — звукоизоляция стояка в коробе без жёсткого контакта с трубой; к арматуре и ревизиям — люк не меньше 300×400.

1000 мм · печать 1:1

Изм.	Кол.уч	Лист	№ док.	Подп.	Дата
Разраб.		Кырлан А.С.			04.11.26
Пров.					
ГИП					
Н. контр.					
Утв.					

ГД-2026-010-АИ

Дом 331 м²

Общая площадь 270,67* м² · * размеры приняты, не замерены (реестр — л. 8–10, К-1)

Дизайн-проект интерьера

Стадия	Лист	Листов
РП	56	216

План выводов сантехники · 1-й этаж

М 1:40

Кырлан Александр Сергеевич


выпуск 04.11.2026 № 2a77323a49 · стр. 58 из 221

План выводов сантехники · Мансарда


Выводы В1, Т3, К1 · привязки от чистовых стен · высоты от чистого пола, мм

ПРЕДВАРИТЕЛЬНО · не для производства работ · открыто пунктов: 15 (реестр — л. 8–10)

Фрагмент 1. Санузел мастер (пом. 15)

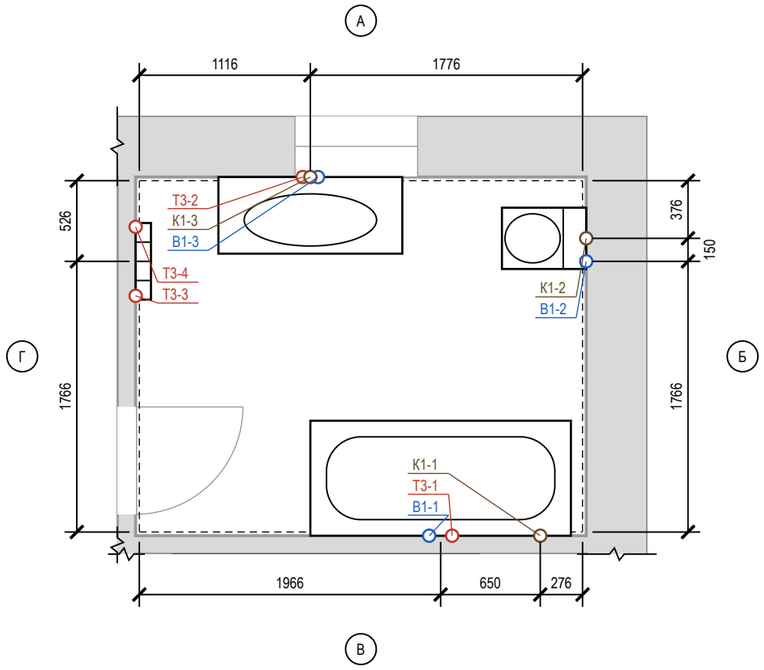

Фрагмент 2. Санузел 2 (пом. 20)

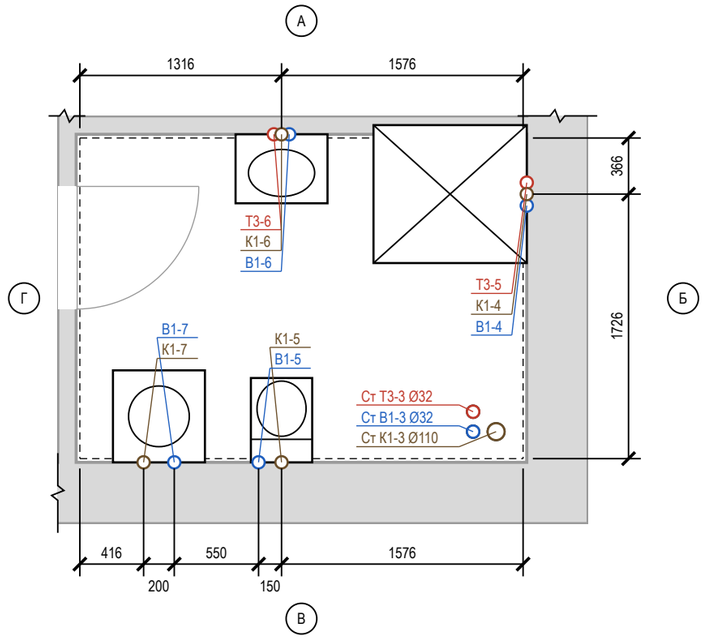

Допущения и предложения на листе

Основа листа: размеры и контуры этажей подобраны проектировщиком по составу помещений и площадям этажей с картинки 470 px (размеры на ней не читаются); обмер и исходный проект — задание (К-1); высоты: 1-й этаж 2800 мм, мансарда 2700 мм (горизонтальная часть) приняты; скаты кровли мансарды приняты по картинке: колено 1200 мм, уклон 45°, конёк вдоль длинной стороны; проект КР — задание (К-2); наружные стены 400 мм, перегородки 120 мм приняты (К-1); разрешённая мощность 15 кВт принята по типовым ТУ для частного дома (К-4); подрайон климата не задан — принят не северный (жилые от 2,5 м) (К-7).
Знак «*» — принято, не замерено и не подтверждено (замерить на объекте): К-2: отметка чистого пола этажа «Мансарда» +3,150 — принята без источника, все отметки мансарды считаются от неё.
Открытые вопросы и конфликты по листу: К-8.
См. лист открытых вопросов (лист 8, записи К-1, К-2, К-4, К-7; лист 9, запись К-8).

Ведомость привязок выводов

Код	Прибор	Ø	H, мм	Привязка от чист. стен, мм	Прим.
В1-1	См1 ванна	½"	800*	ст. В: 1001 от Б	межос. 150
Т3-1	См1 ванна	½"	800*	ст. В: 851 от Б	межос. 150
К1-1	См1 ванна	Ø50	50*	ст. В: 276 от Б	
В1-2	См2 унитаз подвесной	½"	250*	ст. Б: 526 от А	в раме инсталляции
К1-2	См2 унитаз подвесной	Ø110	220*	ст. Б: 376 от А	
В1-3	См3 умывальник	½"	600*	ст. А: 1166 от Г	межос. 100
Т3-2	См3 умывальник	½"	600*	ст. А: 1066 от Г	межос. 100
К1-3	См3 умывальник	Ø50	500*	ст. А: 1116 от Г	
Т3-3	См4 полотенцесушитель	½"	1150*	ст. Г: 751 от А	подача, межос. 450; байпас и краны
Т3-4	См4 полотенцесушитель	½"	1150*	ст. Г: 301 от А	обратка
В1-4	Сд1 душ	½"	1200*	ст. Б: 441 от А	межос. 150
Т3-5	Сд1 душ	½"	1200*	ст. Б: 291 от А	межос. 150
К1-4	Сд1 душ	Ø50	70*	ст. Б: 366 от А	сифон поддона
В1-5	Сд2 унитаз подвесной	½"	250*	ст. В: 1166 от Г	в раме инсталляции
К1-5	Сд2 унитаз подвесной	Ø110	220*	ст. В: 1316 от Г	
В1-6	Сд3 умывальник	½"	600*	ст. А: 1366 от Г	межос. 100
Т3-6	Сд3 умывальник	½"	600*	ст. А: 1266 от Г	межос. 100
К1-6	Сд3 умывальник	Ø50	500*	ст. А: 1316 от Г	
В1-7	Сд4 стиральная машина	½"	600*	ст. В: 616 от Г	кран машины
К1-7	Сд4 стиральная машина	Ø50	600*	ст. В: 416 от Г	

* — высота по практике монтажа; сверить по паспорту прибора

Условные обозначения

- вывод В1 (код — в ведомости привязок)
- вывод Т3 (код — в ведомости привязок)
- вывод К1 (код — в ведомости привязок)
- сантехприбор по расстановке (габарит модели)
- чистовая поверхность стены (от неё привязки)
- стояк «Ст К1-N / Ст В1-N» (ГОСТ 21.601), Ø мм
- линия обрыва (граница фрагмента)
- обозначение стены А–Г (как на развёртках)

Примечания

1. Привязки выводов даны от чистовых поверхностей стен (облицовка на сторону: санузел мастер — 24 мм (штукатурка 10 + клей 5 + плитка 9); санузел 2 24 мм (штукатурка 10 + клей 5 + плитка 9)); эти же грани — на развёртках и в раскладке плитки. Высоты — от чистого пола помещения.
2. Высоты и межосевые, отмеченные «*», приняты по практике монтажа; до черновой разводки сверить по паспорту выбранного прибора (смеситель, инсталляция, сифон).
3. Горячая вода (Т3) — слева от холодной (В1), если смотреть на прибор. Допуск установки выводов: ±5 мм в группе, ±20 мм у отдельно стоящих.
4. Расчёт систем водоснабжения и канализации и подбор оборудования выполняет проектная организация; лист задаёт места и высоты выводов.
5. Стояки в коробах/шахтах не замоноличивать; стояк К1 в коробе — звукоизоляция стояка в коробе без жёсткого контакта с трубой; к арматуре и ревизиям — люк не меньше 300×400.

1000 мм · печать 1:1

Изм.	Кол.уч	Лист	№ док.	Подп.	Дата
Разраб.		Кырлан А.С.			04.11.26
Пров.					
ГИП					
Н. контр.					
Утв.					

ГД-2026-010-АИ

Дом 331 м²

Общая площадь 270,67* м² · * размеры приняты, не замерены (реестр — л. 8–10, К-1)

Дизайн-проект интерьера	Стадия	Лист	Листов
	РП	57	216

План выводов сантехники · Мансарда

М 1:40


Кырлан Александр Сергеевич

выпуск 04.11.2026 № 2a77323a49 · стр. 59 из 221


Схема разводки водопровода и канализации · 1-й этаж

Схемы систем В1, Т3, К1 · трассы принципиальные · уклоны в мм на 1 м · план М 1:400, фрагменты М 1:40

План этажа (М 1:400)

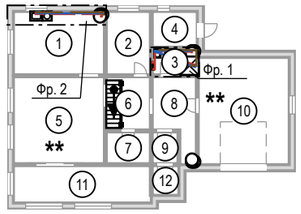


Узел 1. Душ без поддона, трап (Сн1**)

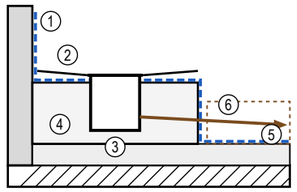

1 гидроизоляция 2 сл. на всю высоту стен душа, по всему санузлу; лента у фланца трапа и в углах
2 плитка, уклон 15 мм/м к трапу (СП 30.13330.2020, п. 17.9)
3 трап с фланцем под гидроизоляцию: монтажная высота 90 мм (до решётки) (принята, по паспорту модели)
4 подиум 100 мм у трапа, ступень 109 мм (ЦПС по гидроизоляции плиты) — предложение, согласовать с заказчиком (К-8)
5 стяжка 35 мм
6 К1 Ø50, i = 25 мм/м, L = 1,70 м, Δh = 42 мм → Ст К1-1; за подиумом — короб 130×110


Пирог ≥ 132 мм = трап 90 + Δh 42 ≤ 35 + подиум 100 + плитка 14 мм

Фр. 1. Санузел 1 этажа (М 1:40)

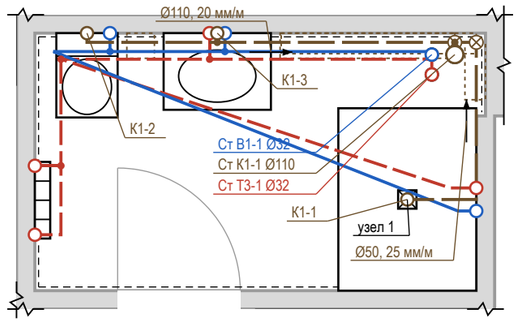

Допущения и предложения на листе. Основа листа: размеры и контуры этажей подобраны проектировщиком по составу помещений и площадям этажей с картинки 470 px (размеры на ней не читаются); обмер и исходный проект — задание (К-1); высоты: 1-й этаж 2800 мм, мансарда 2700 мм (горизонтальная часть) приняты; скаты кровли мансарды приняты по картинке: колено 1200 мм, уклон 45°, конёк вдоль длинной стороны; проект КР — задание (К-2); наружные стены 400 мм, перегородки 120 мм приняты (К-1); разрешённая мощность 15 кВт принята по типовым ТУ для частного дома (К-4); подрайон климата не задан — принят не северный (жилые от 2,5 м) (К-7). Знак «**» — предложение проектировщика, заказчиком не утверждено (согласовать с заказчиком): К-8: Сн1 — Подиум душевой зоны 100 мм — предложение проектировщика: трап в стяжке 35 мм не встаёт (монтажная высота трапа 90 + уклон отвода до стояка 42 = 132 мм). См. лист открытых вопросов (лист 8, записи К-1, К-2, К-4, К-7; лист 9, записи К-8, К-9); по листу — К-8.

Фр. 2. Кухня-столовая (М 1:40)

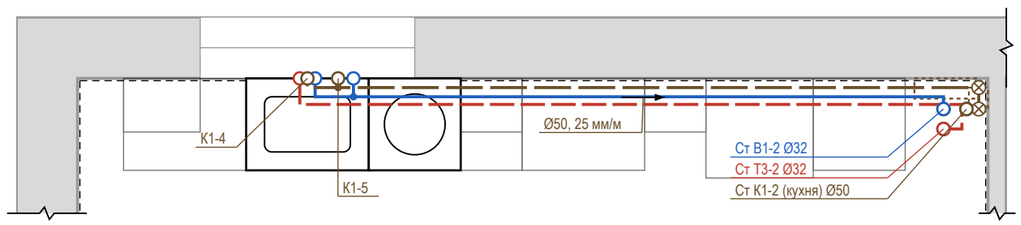

Условные обозначения


- В1 — водопровод хозяйственно-питьевой (ХВС), PP-R Ø20
- Т3 — горячее водоснабжение, подача (ГВС), PP-R Ø20
- К1 — канализация бытовая
- направление уклона К1 / пола: Ø, мм на 1 м
- ⊗ ревизия (прочистка) К1 — доступ сохранить
- • тройник (ответвление к прибору)
- короб К1 над чистым полом (ГКЛВ под плитку)
- ○ вывод В1 (код — в ведомости привязок)
- ○ вывод Т3 (код — в ведомости привязок)
- ○ вывод К1 (код — в ведомости привязок)
- сантехприбор по расстановке (габарит модели)
- ◯ стояк «Ст К1-N / Ст В1-N» (ГОСТ 21.601), Ø мм
- линия обрыва (граница фрагмента)
- граница фрагмента на плане (Фр. N)

Профиль выпусков К1 (до врезки в стояк)

Выпуск	Прибор	Ø	L, м	i, мм/м	Δh, мм	Прокладка, мм
К1-2	Сн2 унитаз подвесной	Ø110	2,54	20	51	короб 200×140
К1-4	Кх1 мойка кухонная	Ø50	4,66	25	117	короб 200×110
К1-1	Сн1** душ	Ø50	1,70	25	42	трап в подиуме 100 (35 + 100 + 14 ≥ 132), далее короб 130×110
К1-3	Сн3 умывальник	Ø50	1,69	25	42	короб 130×110
К1-5	Кх2 посудомоечная машина	Ø40	4,46	30	134	короб 210×110

Короб h×b: h — от чистого пола, b — от чистовой стены. Стяжка 35 мм — лист полов.

Узел ввода В1, Т3 (схема, без масштаба)

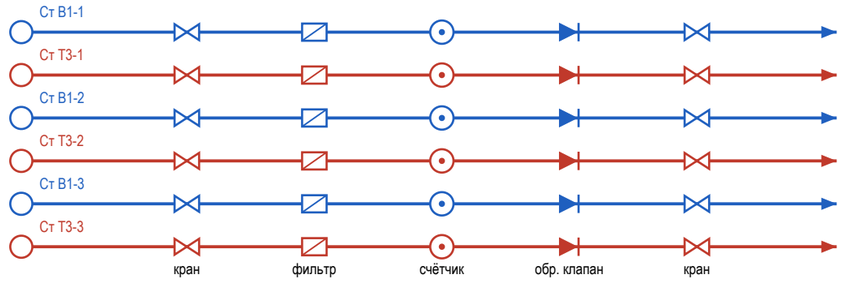

состав узла — по согласованию

⊗ Ст К1-1, Ст К1-2 (кухня), Ст К1-3: ревизия на стояке — люк в коробе

Примечания

1. Трассы принципиальные, построены от стояков вдоль стен помещений; фактическое положение фиксируется исполнительной схемой с привязками (фото с рулеткой) до закрытия.
2. Уклон К1 не менее 1/d и не более 150 мм/м (СП 30.13330.2020, п. 19.1), приняты практические уклоны; поворот — двумя отводами 45°, ревизия после поворота, доступ сохранить. Стояк К1 в коробе — звукоизоляция стояка в коробе, без жёсткого контакта короба с трубой.
3. Решение по К1: стяжка 35 мм не укрывает трубы (нужно Ø + Δh + 45 мм) — выпуски идут над чистым полом вдоль стен; К1-2, К1-4, К1-3, К1-5 — в коробе ГКЛВ под плитку (размеры в профиле). Короба — на развёртках; отметку низа врезки в стояк замерить до черновых работ.
4. К1-1 (Сн1** душ, трап): монтажная высота трапа 90 до верха решётки (по паспорту) + уклон 42 = 132 мм ≤ стяжка 35 + подиум 100 + облицовка 14 мм трап в подиуме душевой зоны (узел 1 на этом листе), за краем подиума отвод — в коробе ГКЛВ 130×110 вдоль стены; подиум — предложение (К-8).
5. Отводы К1-4 (4,7 м), К1-5 (4,5 м) длиннее 4 м без вентиляции — у прибора воздушный клапан Ø50 в доступном месте (за люком или в тумбе) либо вентилируемый отвод (EN 12056-2, табл. 4); предложение проектировщика, подбор — проектная организация.
6. Состав узла ввода В1, Т3 — по согласованию: на схеме типовой узел — кран шаровой, фильтр, счётчик, обратный клапан, кран; состав и места не определены (записи реестра нет). Доступ к арматуре — через люк не меньше 300×400. Водопровод — в штробе стен или в коробах; трубы испытать давлением до закрытия (акт скрытых работ).
7. Расчёт систем, диаметры магистралей и подбор оборудования выполняет проектная организация; положение стояков, выпуск из дома и вентиляция стояков по проекту ВК дома, при его отсутствии — решение владельца с проектной организацией. Арматуру и привязки сверить по паспортам приборов.

Изм.	Кол.уч	Лист	№ док.	Подп.	Дата
Разраб.		Кырлан А.С.			04.11.26
Пров.					
ГИП					
Н. контр.					
Утв.					

ГД-2026-010-АИ

Дом 331 м²

Общая площадь 270,67* м² · * размеры приняты, не замерены (реестр — л. 8–10, К-1)

Дизайн-проект интерьера

Стадия	Лист	Листов
РП	58	216

Схема разводки водопровода и канализации · 1-й этаж
М 1:400; 1:40

Кырлан Александр Сергеевич


выпуск 04.11.2026 № 2a77323a49 · стр. 60 из 221

Схема разводки водопровода и канализации · Мансарда


Схемы систем В1, Т3, К1 · трассы принципиальные · уклоны в мм на 1 м · план М 1:200, фрагменты М 1:40

ПРЕДВАРИТЕЛЬНО · не для производства работ · открыто пунктов: 15 (реестр — л. 8–10)


План этажа (М 1:200)

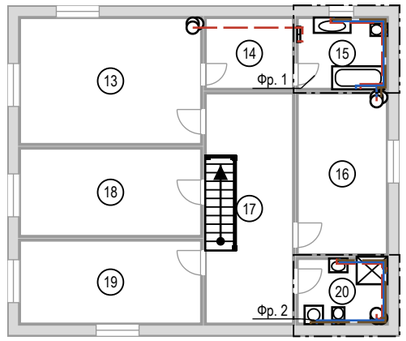

Фр. 1. Санузел мастер (М 1:40)

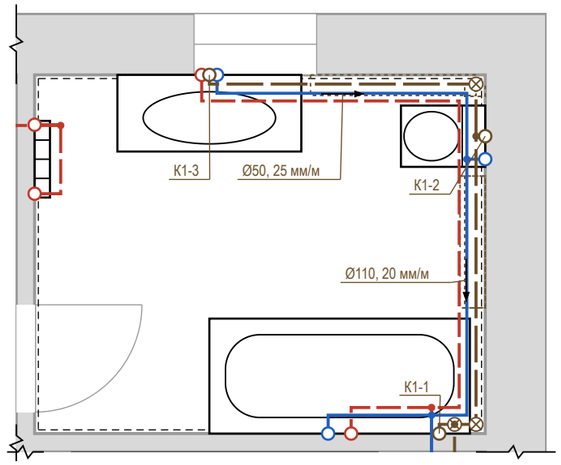

Фр. 2. Санузел 2 (М 1:40)

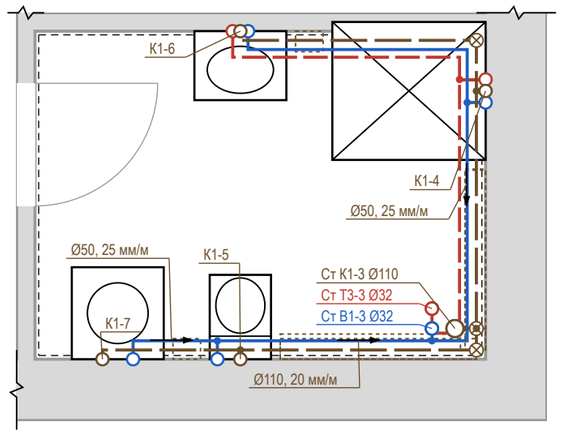

Условные обозначения


- В1 — водопровод хозяйственно-питьевой (ХВС), PP-R Ø20
- Т3 — горячее водоснабжение, подача (ГВС), PP-R Ø20
- К1 — канализация бытовая
- направление уклона К1 / пола: Ø, мм на 1 м
- ревизия (прочистка) К1 — доступ сохранить
- тройник (ответвление к прибору)
- короб К1 над чистым полом (ГКЛВ под плитку)
- вывод В1 (код — в ведомости привязок)
- вывод Т3 (код — в ведомости привязок)
- вывод К1 (код — в ведомости привязок)
- сантехприбор по расстановке (габарит модели)
- стояк «Ст К1-N / Ст В1-N» (ГОСТ 21.601), Ø мм
- линия обрыва (граница фрагмента)
- граница фрагмента на плане (Фр. N)

Профиль выпусков К1 (до врезки в стояк)

Выпуск	Прибор	Ø	L, м	i, мм/м	Δh, мм	Прокладка, мм
К1-2	См2 унитаз подвесной	Ø110	2,40	20	48	короб 190×140
К1-5	Сд2 унитаз подвесной	Ø110	1,88	20	38	короб 180×140
К1-3	См3 умывальник	Ø50	4,48	25	112	короб 200×110
К1-6	Сд3 умывальник	Ø50	3,62	25	91	короб 180×110
К1-7	Сд4 стиральная машина	Ø50	2,78	25	70	короб 150×110
К1-4	Сд1 душ	Ø50	1,75	25	44	короб 130×110
К1-1	См1 ванна	Ø50	0,48	25	12	над полом за приборами

Короб h×b: h — от чистого пола, b — от чистовой стены. Стяжка 35 мм — лист полов.

Узел ввода В1, Т3 (схема, без масштаба)

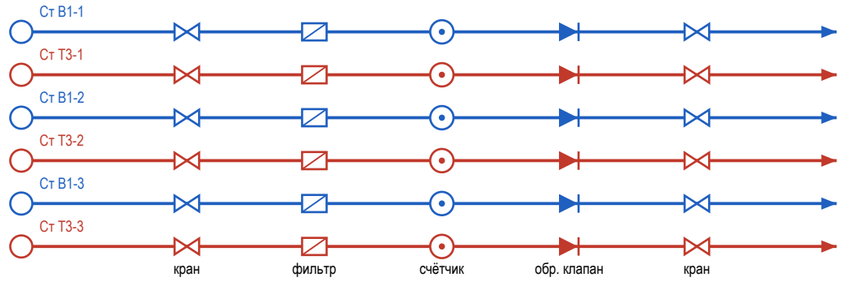

состав узла — по согласованию

⊗ Ст К1-1, Ст К1-2 (кухня), Ст К1-3: ревизия на стояке — люк в коробе

Допущения и предложения на листе

Основа листа: размеры и контуры этажей подобраны проектировщиком по составу помещений и площадям этажей с картинки 470 px (размеры на ней не читаются); обмер и исходный проект — задание (К-1); высоты: 1-й этаж 2800 мм, мансарда 2700 мм (горизонтальная часть) приняты; скаты кровли мансарды приняты по картинке: колено 1200 мм, уклон 45°, конёк вдоль длинной стороны; проект КР — задание (К-2); наружные стены 400 мм, перегородки 120 мм приняты (К-1); разрешённая мощность 15 кВт принята по типовым ТУ для частного дома (К-4); подрайон климата не задан — принят не северный (жилые от 2,5 м) (К-7).

Знак «*» — принято, не замерено и не подтверждено (замерить на объекте): К-2: отметка чистого пола этажа «Мансарда» +3,150 — принята без источника, все отметки мансарды считаются от неё.

Открытые вопросы и конфликты по листу: К-8.

См. лист открытых вопросов (лист 8, записи К-1, К-2, К-4, К-7; лист 9, запись К-8).

Примечания

1. Трассы принципиальные, построены от стояков вдоль стен помещений; фактическое положение фиксируется исполнительной схемой с привязками (фото с рулеткой) до закрытия.
2. Уклон К1 не менее 1/d и не более 150 мм/м (СП 30.13330.2020, п. 19.1), приняты практические уклоны; поворот — двумя отводами 45°, ревизия после поворота, доступ сохранить. Стояк К1 в коробе — звукоизоляция стояка в коробе, без жёсткого контакта короба с трубой.
3. Решение по К1: стяжка 35 мм не укрывает трубы (нужно Ø + Δh + 45 мм) — выпуски идут над чистым полом вдоль стен: К1-1 — за приборами и в раме инсталляции; К1-2, К1-5, К1-3, К1-6, К1-7, К1-4 — в коробе ГКЛВ под плитку (размеры в профиле). Короба — на развёртках; отметку низа врезки в стояк замерить до черновых работ.
4. Отводы К1-3 (4,5 м) длиннее 4 м без вентиляции — у прибора воздушный клапан Ø50 в доступном месте (за люком или в тумбе) либо вентилируемый отвод (EN 12056-2, табл. 4); предложение проектировщика, подбор — проектная организация.
5. Состав узла ввода В1, Т3 — по согласованию: на схеме типовой узел — кран шаровой, фильтр, счётчик, обратный клапан, кран; состав и места не определены (записи реестра нет). Доступ к арматуре — через люк не меньше 300×400. Водопровод — в штробе стен или в коробах; трубы испытать давлением до закрытия (акт скрытых работ).
6. Расчёт систем, диаметры магистралей и подбор оборудования выполняет проектная организация; положение стояков, выпуск из дома и вентиляция стояков по проекту ВК дома, при его отсутствии — решение владельца с проектной организацией. Арматуру и привязки сверить по паспортам приборов.


Изм.	Кол.уч	Лист	№ док.	Подп.	Дата				
Разраб.		Кырлан А.С.			04.11.26	**ГД-2026-010-АИ**			
Пров.						Дом 331 м²			
ГИП						Общая площадь 270,67* м² · * размеры приняты, не замерены (реестр — л. 8–10, К-1)			
						Дизайн-проект интерьера	Стадия	Лист	Листов
Н. контр.							РП	59	216
Утв.						**Схема разводки водопровода и канализации · Мансарда** М 1:200; 1:40	**Кырлан Александр Сергеевич**		

выпуск 04.11.2026 № 2a7732a49 · стр. 61 из 221

Аксонометрическая схема В1 (холодное водоснабжение)

аксонометрия · диаметры, уклоны, отметки, стояки и приборы · трассы принципиальные

Схема В1 (М 1:100; по вертикали и горизонтали один масштаб, глубина — ×0,5 под 45°)

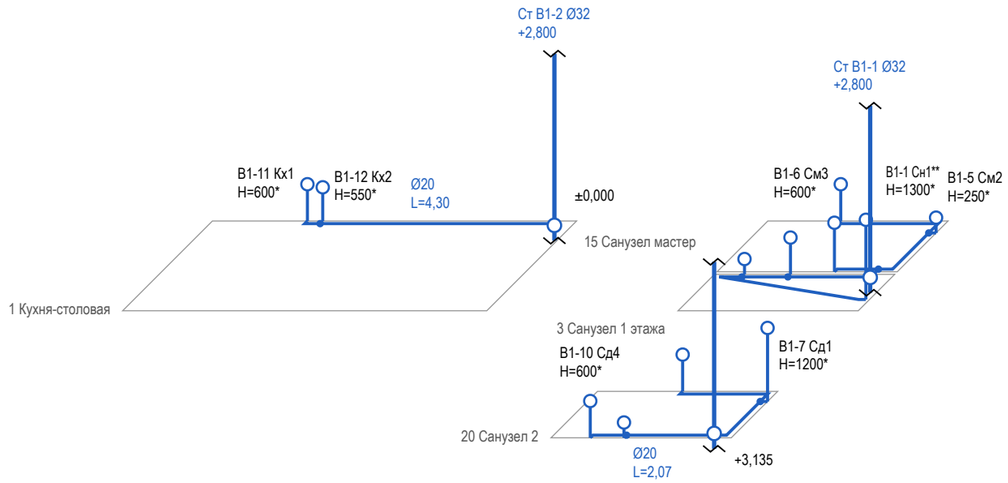

Условные обозначения

- В1 — водопровод хозяйственно-питьевой (ХВС), PP-R Ø20
- вывод В1 (код — в ведомости привязок)
- стояк «Ст К1-N / Ст В1-N» (ГОСТ 21.601), Ø мм
- стояк в плане (на отметке пола); вертикаль — стояк по высоте, разрыв — перекрытие
- тройник (ответвление к прибору)
- кран шаровой

Допущения и предложения на листе

Основа листа: размеры и контуры этажей подобраны проектировщиком по составу помещений и площадям этажей с картинки 470 px (размеры на ней не читаются); обмер и исходный проект — задание (К-1); высоты: 1-й этаж 2800 мм, мансарда 2700 мм (горизонтальная часть) приняты; скаты кровли мансарды приняты по картинке: колено 1200 мм, уклон 45°, конёк вдоль длинной стороны; проект КР — задание (К-2); наружные стены 400 мм, перегородки 120 мм приняты (К-1); разрешённая мощность 15 кВт принята по типовым ТУ для частного дома (К-4); подрайон климата не задан — принят не северный (жилые от 2,5 м) (К-7).

Знак «**» — предложение проектировщика, заказчиком не утверждено (согласовать с заказчиком): К-8: Сн1 — Подиум душевой зоны 100 мм — предложение проектировщика: трап в стяжке 35 мм не встаёт (монтажная высота трапа 90 + уклон отвода до стояка 42 = 132 мм).

См. лист открытых вопросов (лист 8, записи К-1, К-2, К-4, К-7; лист 9, запись К-8).

Примечания

1. Схема В1 построена по тем же трассам, что план разводки: положение в плане сохранено, глубина — в масштабе ×0,5. Трассы принципиальные; фактическое положение фиксируется исполнительной схемой до закрытия.
2. Высоты Н — от чистого пола помещения, мм. Отметка прокладки магистрали В1 (в стяжке, в стене или по полу) в данных не задана: участки показаны на уровне пола условно (записи реестра нет).
3. * — высота вывода принята по практике монтажа; сверить по паспорту прибора.
4. Узел ввода В1 (кран, фильтр, счётчик, обратный клапан, кран) — на схеме разводки; состав узла ввода — по согласованию. Кран шаровой — на первом участке от стояка.
5. Трубы испытать давлением до закрытия (акт скрытых работ, опрессовка по СП 73.13330.2016).
6. Диаметры, высоты выводов и места кранов — по паспортам выбранных приборов и расчёту проектной организации.
7. Расчёт систем, диаметры магистралей и подбор оборудования выполняет проектная организация.

1000 мм · печать 1:1

Изм.	Кол.уч	Лист	№ док.	Подп.	Дата
Разраб.		Кырлан А.С.			04.11.26
Пров.					
ГИП					
Н. контр.					
Утв.					

ГД-2026-010-АИ

Дом 331 м²

Общая площадь 270,67* м² · * размеры приняты, не замерены (реестр — л. 8–10, К-1)

Дизайн-проект интерьера

Стадия	Лист	Листов
РП	60	216

Аксонометрическая схема В1 (холодное водоснабжение)

М 1:100

Кырлан Александр Сергеевич


ПРЕДВАРИТЕЛЬНО · не для производства работ · открыто пунктов: 15 (реестр — л. 8–10)

выпуск 04.11.2026 № 2a77323a49 · стр. 62 из 221

Аксонометрическая схема Т3 (горячее водоснабжение)

аксонометрия · диаметры, уклоны, отметки, стояки и приборы · трассы принципиальные

Схема Т3 (М 1:100; по вертикали и горизонтали один масштаб, глубина — ×0,5 под 45°)

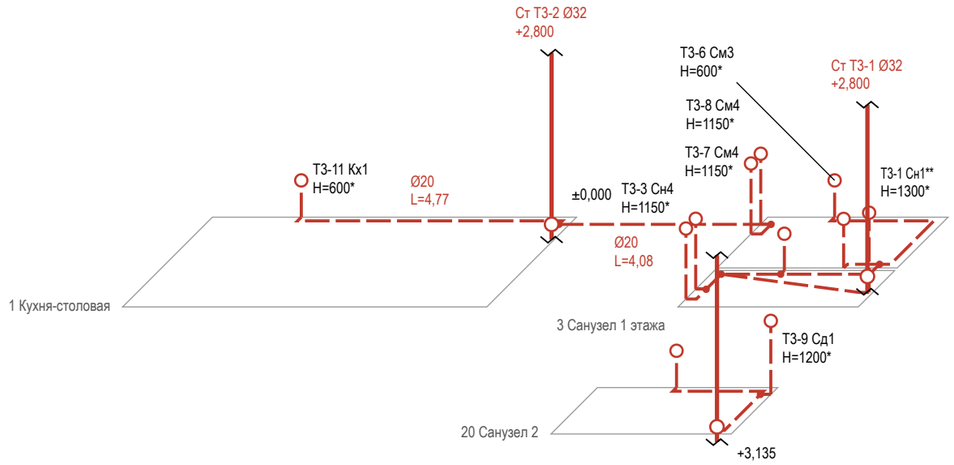

ПРЕДВАРИТЕЛЬНО · не для производства работ · открыто пунктов: 15 (реестр — л. 8–10)

Условные обозначения

- Т3 — горячее водоснабжение, подача (ГВС), PP-R Ø20
- вывод Т3 (код — в ведомости привязок)
- стояк «Ст К1-N / Ст В1-N» (ГОСТ 21.601), Ø мм
- стояк в плане (на отметке пола); вертикаль — стояк по высоте, разрыв — перекрытие
- тройник (ответвление к прибору)
- кран шаровой

Допущения и предложения на листе

Основа листа: размеры и контуры этажей подобраны проектировщиком по составу помещений и площадям этажей с картинки 470 px (размеры на ней не читаются); обмер и исходный проект — задание (К-1); высоты: 1-й этаж 2800 мм, мансарда 2700 мм (горизонтальная часть) приняты; скаты кровли мансарды приняты по картинке: колено 1200 мм, уклон 45°, конёк вдоль длинной стороны; проект КР — задание (К-2); наружные стены 400 мм, перегородки 120 мм приняты (К-1); разрешённая мощность 15 кВт принята по типовым ТУ для частного дома (К-4); подрайон климата не задан — принят не северный (жилые от 2,5 м) (К-7).

Знак «**» — предложение проектировщика, заказчиком не утверждено (согласовать с заказчиком): К-8: Сн1 — Подиум душевой зоны 100 мм — предложение проектировщика: трап в стяжке 35 мм не встаёт (монтажная высота трапа 90 + уклон отвода до стояка 42 = 132 мм).

См. лист открытых вопросов (лист 8, записи К-1, К-2, К-4, К-7; лист 9, запись К-8).

Примечания

1. Схема Т3 построена по тем же трассам, что план разводки: положение в плане сохранено, глубина — в масштабе ×0,5. Трассы принципиальные; фактическое положение фиксируется исполнительной схемой до закрытия.
2. Высоты Н — от чистого пола помещения, мм. Отметка прокладки магистрали Т3 (в стяжке, в стене или по полу) в данных не задана: участки показаны на уровне пола условно (записи реестра нет).
3. * — высота вывода принята по практике монтажа; сверить по паспорту прибора.
4. Узел ввода Т3 (кран, фильтр, счётчик, обратный клапан, кран) — на схеме разводки; состав узла ввода — по согласованию. Кран шаровой — на первом участке от стояка.
5. Циркуляция ГВС в данных не задана — циркуляционного трубопровода на схеме нет (записи реестра нет).
6. Трубы испытать давлением до закрытия (акт скрытых работ, опрессовка по СП 73.13330.2016).
7. Диаметры, высоты выводов и места кранов — по паспортам выбранных приборов и расчёту проектной организации.
8. Расчёт систем, диаметры магистралей и подбор оборудования выполняет проектная организация.

1000 мм · печать 1:1

Изм.	Кол.уч	Лист	№ док.	Подп.	Дата
Разраб.		Кырлан А.С.			04.11.26
Пров.					
ГИП					
Н. контр.					
Утв.					

ГД-2026-010-АИ

Дом 331 м²

Общая площадь 270,67* м² · * размеры приняты, не замерены (реестр — л. 8–10, К-1)

Дизайн-проект интерьера

Стадия	Лист	Листов
РП	61	216

Аксонометрическая схема Т3 (горячее водоснабжение)

М 1:100


Кырлан Александр Сергеевич

выпуск 04.11.2026 № 2a77323a49 · стр. 63 из 221

Аксонометрическая схема К1 (канализация)

аксонометрия · диаметры, уклоны, отметки, стояки и приборы · трассы принципиальные

Схема К1 (М 1:100; по вертикали и горизонтали один масштаб, глубина — ×0,5 под 45°)

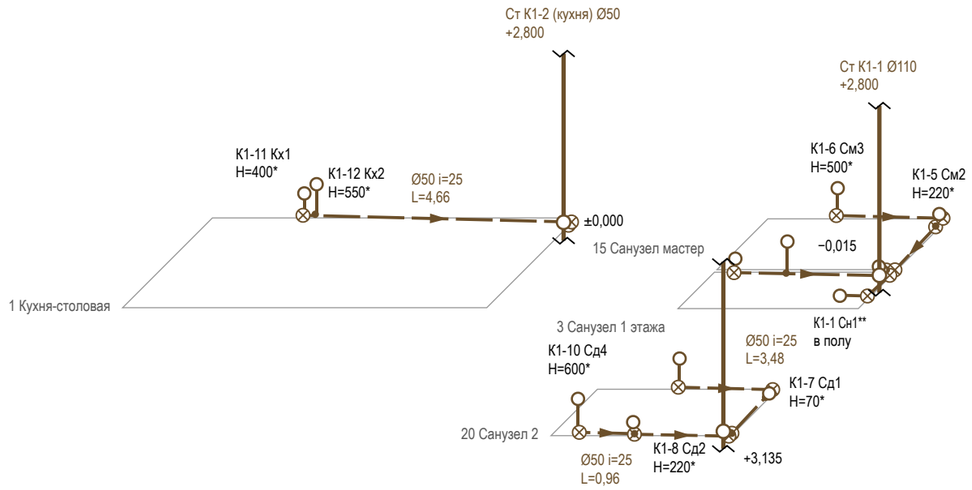

ПРЕДВАРИТЕЛЬНО · не для производства работ · открыто пунктов: 15 (реестр — л. 8–10)

Условные обозначения

- К1 — канализация бытовая
- вывод К1 (код — в ведомости привязок)
- стояк «Ст К1-N / Ст В1-N» (ГОСТ 21.601), Ø мм
- стояк в плане (на отметке пола); вертикаль — стояк по высоте, разрыв — перекрытие
- направление уклона К1 / пола: Ø, мм на 1 м
- ревизия (прочистка) К1 — доступ сохранить
- тройник (ответвление к прибору)

Допущения и предложения на листе

Основа листа: размеры и контуры этажей подобраны проектировщиком по составу помещений и площадям этажей с картинки 470 px (размеры на ней не читаются); обмер и исходный проект — задание (К-1); высоты: 1-й этаж 2800 мм, мансарда 2700 мм (горизонтальная часть) приняты; скаты кровли мансарды приняты по картинке: колено 1200 мм, уклон 45°, конёк вдоль длинной стороны; проект КР — задание (К-2); наружные стены 400 мм, перегородки 120 мм приняты (К-1); разрешённая мощность 15 кВт принята по типовым ТУ для частного дома (К-4); подрайон климата не задан — принят не северный (жилые от 2,5 м) (К-7).

Знак «**» — предложение проектировщика, заказчиком не утверждено (согласовать с заказчиком): К-8: Сн1 — Подиум душевой зоны 100 мм — предложение проектировщика: трап в стяжке 35 мм не встаёт (монтажная высота трапа 90 + уклон отвода до стояка 42 = 132 мм).

См. лист открытых вопросов (лист 8, записи К-1, К-2, К-4, К-7; лист 9, запись К-8).

Примечания

1. Схема К1 построена по тем же трассам, что план разводки: положение в плане сохранено, глубина — в масштабе ×0,5. Трассы принципиальные; фактическое положение фиксируется исполнительной схемой до закрытия.
2. Отметки — от плиты перекрытия: низ трубы у врезки в стояк — отметка из данных выпуска, к прибору труба поднимается на уклон i, мм/м (уклон не менее 1/d и не более 150 мм/м, СП 30.13330.2020, п. 19.1); чистый пол — выше плиты на стяжку (высота пирога пола). Высота выпуска прибора H — от чистого пола.
3. * — высота вывода принята по практике монтажа; сверить по паспорту прибора.
4. Ревизия — на повороте и в начале участка; стояк К1 в коробе с люком — звукоизоляция стояка в коробе; поворот — двумя отводами 45°.
5. Трубы испытать давлением до закрытия (акт скрытых работ, опрессовка по СП 73.13330.2016).
6. Диаметры, высоты выводов и места кранов — по паспортам выбранных приборов и расчёту проектной организации.
7. Расчёт систем, диаметры магистралей и подбор оборудования выполняет проектная организация.

1000 мм · печать 1:1

Изм.	Кол.уч	Лист	№ док.	Подп.	Дата
Разраб.		Кырлан А.С.			04.11.26
Пров.					
ГИП					
Н. контр.					
Утв.					

ГД-2026-010-АИ

Дом 331 м²

Общая площадь 270,67* м² · * размеры приняты, не замерены (реестр — л. 8–10, К-1)

Дизайн-проект интерьера

Стадия	Лист	Листов
РП	62	216

Аксонометрическая схема К1 (канализация)

М 1:100


Кырлан Александр Сергеевич

выпуск 04.11.2026 № 2a77323a49 · стр. 64 из 221

Развёртки мокрых зон: выводы ВК. Кухня-столовая

пом. 1 · выводы В1, Т3, К1 на стенах · высоты от чистого пола, привязки от чистовых углов, мм

Стена А (М 1:25)

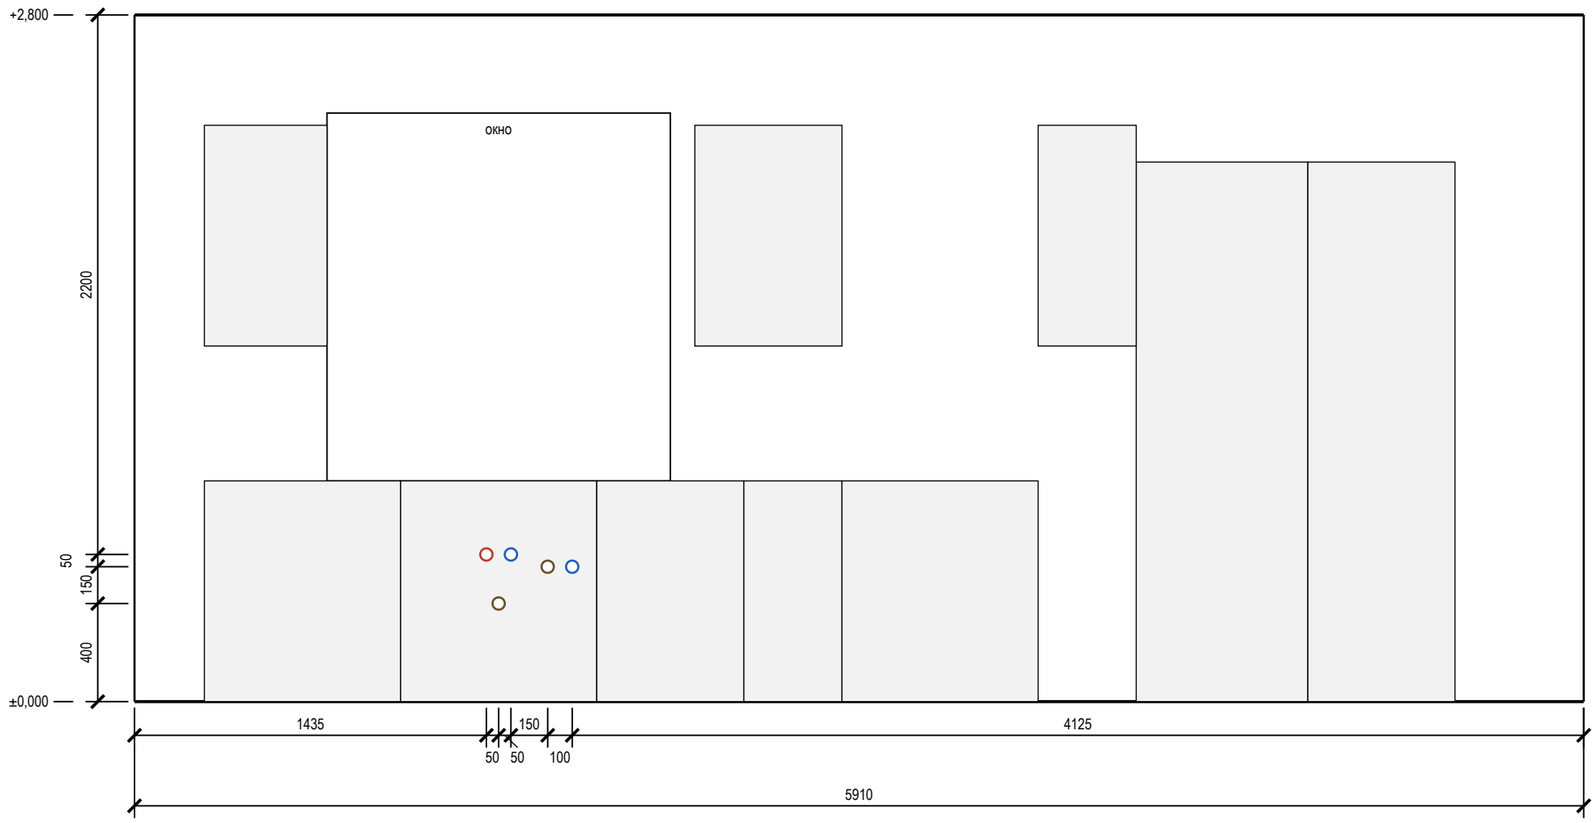

Допущения и предложения на листе

Основа листа: размеры и контуры этажей подобраны проектировщиком по составу помещений и площадям этажей с картинки 470 px (размеры на ней не читаются); обмер и исходный проект — задание (К-1); высоты: 1-й этаж 2800 мм, мансарда 2700 мм (горизонтальная часть) приняты; скаты кровли мансарды приняты по картинке: колено 1200 мм, уклон 45°, конёк вдоль длинной стороны; проект КР — задание (К-2); наружные стены 400 мм, перегородки 120 мм приняты (К-1); разрешённая мощность 15 кВт принята по типовым ТУ для частного дома (К-4); подрайон климата не задан — принят не северный (жилые от 2,5 м) (К-7).
См. лист открытых вопросов (лист 8, записи К-1, К-2, К-4, К-7).

Ведомость привязок выводов (от чистого пола и угла)

Код	Прибор	Ø	H, мм	Привязка, мм
В1-11	Кх1 мойка кухонная	½"	600*	ст. А: 1535 от лев. угла
Т3-11	Кх1 мойка кухонная	½"	600*	ст. А: 1435 от лев. угла
К1-11	Кх1 мойка кухонная	Ø50	400*	ст. А: 1485 от лев. угла
В1-12	Кх2 посудомоечная машина	½"	550*	ст. А: 1785 от лев. угла
К1-12	Кх2 посудомоечная машина	Ø40	550*	ст. А: 1685 от лев. угла

Условные обозначения

- вывод В1 (код — в ведомости привязок)
- вывод Т3 (код — в ведомости привязок)
- вывод К1 (код — в ведомости привязок)
- сантехприбор по расстановке (габарит модели)
- дверной проём; окно — сплошной контур

Примечания

1. Габариты и высоты приборов, межосевые смесителей и места кранов — по паспортам выбранных приборов, сверяются до разметки стен.
2. Высоты H — от чистого пола помещения, мм; отметка чистого пола и потолка — у левого края вида (от ±0,000 объекта). Привязки — от левого чистового угла вида (облицовка стен вычтена), как на развёртках стен.
3. * — высота принята по практике монтажа: в данных прибора её нет; до разметки стен сверить по паспорту выбранного прибора (смеситель, инсталляция, сифон).
4. Стояки в помещении: Ст К1-2 (кухня) Ø50, Ст В1-2 Ø32, Ст Т3-2 Ø32 — положение на плане выводов; выводы подключаются к ним по схеме разводки.
5. Ревизионные люки к арматуре и ревизиям в данных не заданы: место и размер не определены (записи реестра нет).
6. Мойка, ПММ и фильтр — выводы в шкафу мойки; диаметры и положение сифона и кранов сверить по паспортам приборов и чертежам модуля.
7. Часть подписей выводов не уместилась у знака: коды и высоты — в ведомости привязок.
8. Расчёт систем водоснабжения и канализации и подбор оборудования выполняет проектная организация; лист задаёт места и высоты выводов.

1000 мм · печать 1:1

Изм.	Кол.уч	Лист	№ док.	Подп.	Дата
Разраб.		Кырлан А.С.			04.11.26
Пров.					
ГИП					
Н. контр.					
Утв.					

ГД-2026-010-АИ

Дом 331 м²

Общая площадь 270,67* м² · * размеры приняты, не замерены (реестр — л. 8–10, К-1)

Дизайн-проект интерьера

Стадия	Лист	Листов
РП	63	216

Развёртки мокрых зон: выводы ВК. Кухня-столовая
М 1:25


Кырлан Александр Сергеевич

Развёртки мокрых зон: выводы ВК. Санузел 1 этажа (лист 1 из 2)


пом. 3 · выводы В1, Т3, К1 на стенах · высоты от чистого пола, привязки от чистовых углов, мм

ПРЕДВАРИТЕЛЬНО · не для производства работ · открыто пунктов: 15 (реестр — л. 8–10)

Стена А (М 1:20)

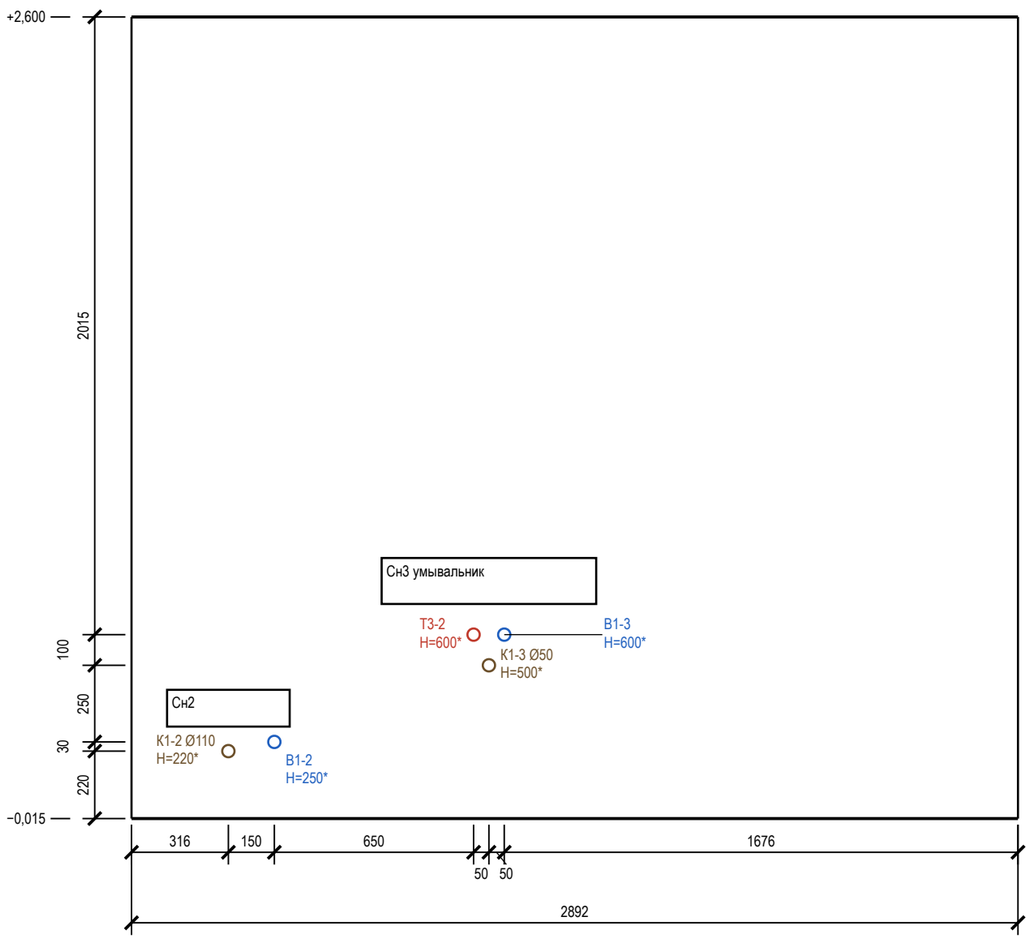

Стена Б (М 1:20)

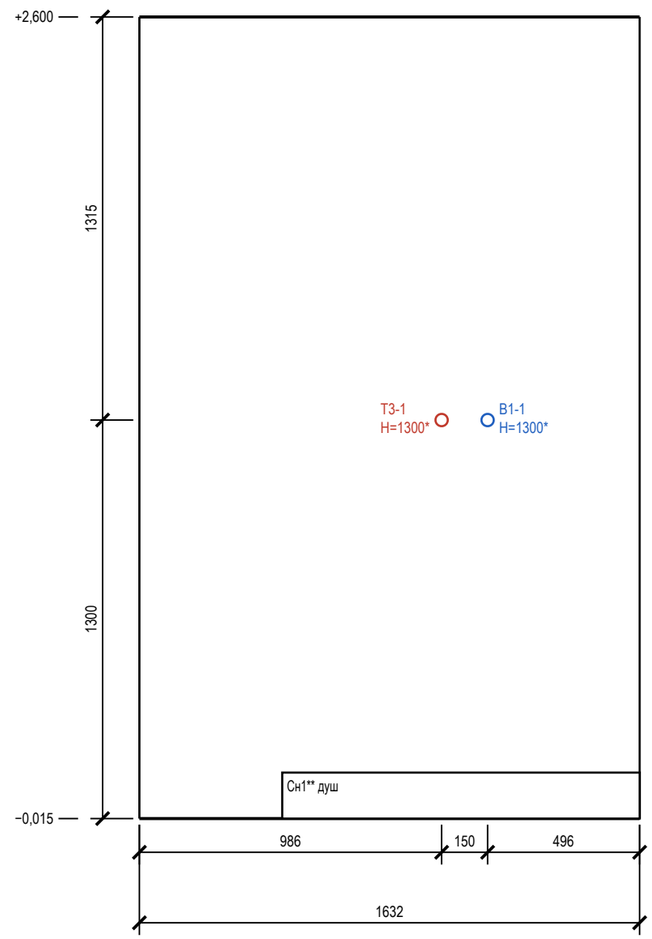

Допущения и предложения на листе

Основа листа: размеры и контуры этажей подобраны проектировщиком по составу помещений и площадям этажей с картинки 470 px (размеры на ней не читаются); обмер и исходный проект — задание (К-1); высоты: 1-й этаж 2800 мм, мансарда 2700 мм (горизонтальная часть) приняты; скаты кровли мансарды приняты по картинке: колено 1200 мм, уклон 45°, конёк вдоль длинной стороны; проект КР — задание (К-2); наружные стены 400 мм, перегородки 120 мм приняты (К-1); разрешённая мощность 15 кВт принята по типовым ТУ для частного дома (К-4); подрайон климата не задан — принят не северный (жилые от 2,5 м) (К-7).

Знак «**» — предложение проектировщика, заказчиком не утверждено (согласовать с заказчиком): К-8: Сн1 — Подиум душевой зоны 100 мм — предложение проектировщика: трап в стяжке 35 мм не встаёт (монтажная высота трапа 90 + уклон отвода до стояка 42 = 132 мм).

См. лист открытых вопросов (лист 8, записи К-1, К-2, К-4, К-7; лист 9, запись К-8).

Ведомость привязок выводов (от чистого пола и угла)

Код	Прибор	Ø	H, мм	Привязка, мм
В1-2	Сн2 унитаз подвесной	½"	250*	ст. А: 466 от лев. угла
К1-2	Сн2 унитаз подвесной	Ø110	220*	ст. А: 316 от лев. угла
В1-3	Сн3 умывальник	½"	600*	ст. А: 1216 от лев. угла
Т3-2	Сн3 умывальник	½"	600*	ст. А: 1116 от лев. угла

Ведомость привязок (продолжение)

Код	Прибор	Ø	H, мм	Привязка, мм
К1-3	Сн3 умывальник	Ø50	500*	ст. А: 1166 от лев. угла
В1-1	Сн1** душ	½"	1300*	ст. Б: 1136 от лев. угла
Т3-1	Сн1** душ	½"	1300*	ст. Б: 986 от лев. угла

Условные обозначения

- вывод В1 (код — в ведомости привязок)
- вывод Т3 (код — в ведомости привязок)
- вывод К1 (код — в ведомости привязок)
- сантехприбор по расстановке (габарит модели)
- дверной проём; окно — сплошной контур

Примечания

1. Габариты и высоты приборов, межосевые смесителей и места кранов — по паспортам выбранных приборов, сверяются до разметки стен.
2. Высоты H — от чистого пола помещения, мм; отметка чистого пола и потолка — у левого края вида (от ±0,000 объекта). Привязки — от левого чистового угла вида (облицовка стен вычтена), как на развёртках стен.
3. * — высота принята по практике монтажа: в данных прибора её нет; до разметки стен сверить по паспорту выбранного прибора (смеситель, инсталляция, сифон).
4. Выводы в полу (К1-1): трап, лоток, выпуск отдельностоящей ванны, подвод к стойке напольного смесителя — на развёртке их нет; место и пирог пола лист «Схема разводки» (профиль К1, узел 1).
5. Стояки в помещении: Ст К1-1 Ø110, Ст В1-1 Ø32, Ст Т3-1 Ø32 — положение на плане выводов; выводы подключаются к ним по схеме разводки.
6. Ревизионные люки к арматуре и ревизиям в данных не заданы: место и размер не определены (записи реестра нет).
7. Помещение «Санузел 1 этажа» — 2 листа: стены 1) А, Б; 2) В, Г.
8. Расчёт систем водоснабжения и канализации и подбор оборудования выполняет проектная организация; лист задаёт места и высоты выводов.

1000 мм · печать 1:1

Изм.	Кол.уч	Лист	№ док.	Подп.	Дата
Разраб.		Кырлан А.С.			04.11.26
Пров.					
ГИП					
Н. контр.					
Утв.					

ГД-2026-010-АИ

Дом 331 м²

Общая площадь 270,67* м² · * размеры приняты, не замерены (реестр — л. 8–10, К-1)

Дизайн-проект интерьера

Стадия	Лист	Листов
РП	64	216

Развёртки мокрых зон: выводы ВК. Санузел 1 этажа (лист 1 из 2)

М 1:20

Кырлан Александр Сергеевич


выпуск 04.11.2026 № 2a77323a49 · стр. 66 из 221

Развёртки мокрых зон: выводы ВК. Санузел 1 этажа (лист 2 из 2)


пом. 3 · выводы В1, Т3, К1 на стенах · высоты от чистого пола, привязки от чистовых углов, мм

ПРЕДВАРИТЕЛЬНО · не для производства работ · открыто пунктов: 15 (реестр — л. 8–10)

Стена В (М 1:20)

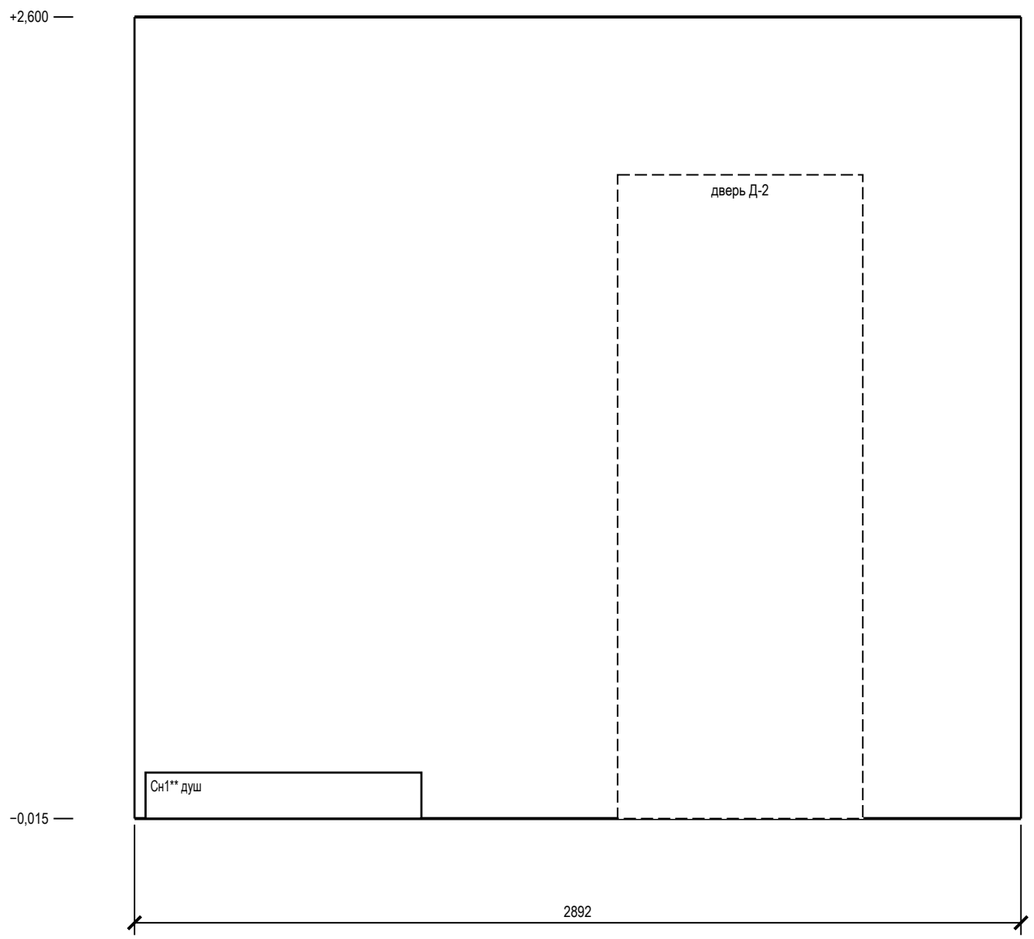

Стена Г (М 1:20)

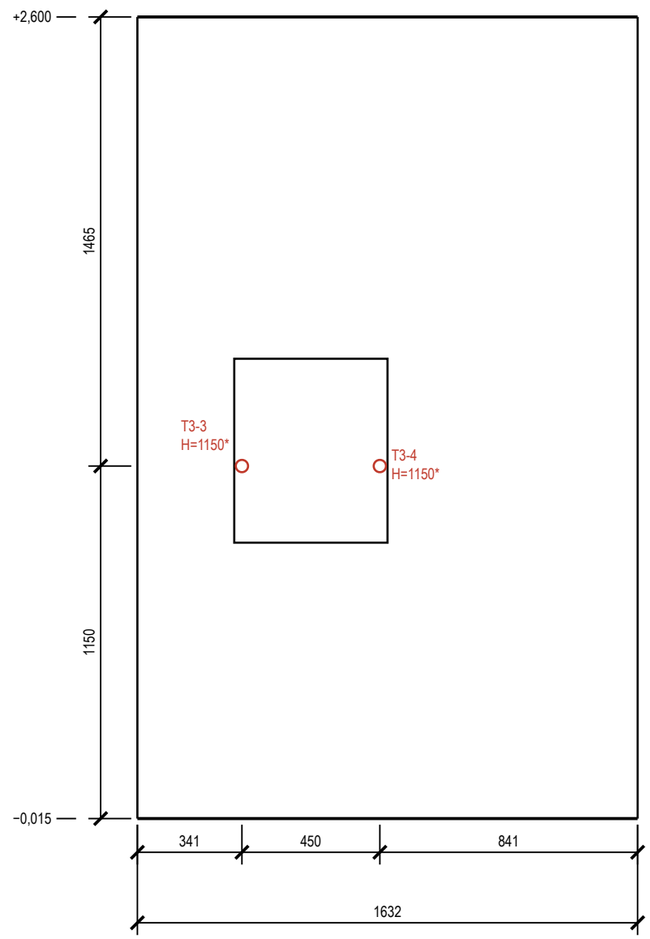

Допущения и предложения на листе

Основа листа: размеры и контуры этажей подобраны проектировщиком по составу помещений и площадям этажей с картинки 470 px (размеры на ней не читаются); обмер и исходный проект — задание (К-1); высоты: 1-й этаж 2800 мм, мансарда 2700 мм (горизонтальная часть) приняты; скаты кровли мансарды приняты по картинке: колено 1200 мм, уклон 45°, конёк вдоль длинной стороны; проект КР — задание (К-2); наружные стены 400 мм, перегородки 120 мм приняты (К-1); разрешённая мощность 15 кВт принята по типовым ТУ для частного дома (К-4); подрайон климата не задан — принят не северный (жилые от 2,5 м) (К-7).

Знак «**» — предложение проектировщика, заказчиком не утверждено (согласовать с заказчиком): К-8: Сн1 — Подиум душевой зоны 100 мм — предложение проектировщика: трап в стяжке 35 мм не встаёт (монтажная высота трапа 90 + уклон отвода до стояка 42 = 132 мм).

См. лист открытых вопросов (лист 8, записи К-1, К-2, К-4, К-7; лист 9, запись К-8).

Ведомость привязок выводов (от чистого пола и угла)

Код	Прибор	Ø	H, мм	Привязка, мм
Т3-3	Сн4 полотенцесушитель	½"	1150*	ст. Г: 341 от лев. угла
Т3-4	Сн4 полотенцесушитель	½"	1150*	ст. Г: 791 от лев. угла

Условные обозначения

- вывод В1 (код — в ведомости привязок)
- вывод Т3 (код — в ведомости привязок)
- вывод К1 (код — в ведомости привязок)
- сантехприбор по расстановке (габарит модели)
- дверной проём; окно — сплошной контур

Примечания

1. Габариты и высоты приборов, межосевые смесителей и места кранов — по паспортам выбранных приборов, сверяются до разметки стен.
2. Высоты H — от чистого пола помещения, мм; отметка чистого пола и потолка — у левого края вида (от ±0,000 объекта). Привязки — от левого чистового угла вида (облицовка стен вычтена), как на развёртках стен.
3. * — высота принята по практике монтажа: в данных прибора её нет; до разметки стен сверить по паспорту выбранного прибора (смеситель, инсталляция, сифон).
4. Выводы в полу (К1-1): трап, лоток, выпуск отдельностоящей ванны, подвод к стойке напольного смесителя — на развёртке их нет; место и пирог пола лист «Схема разводки» (профиль К1, узел 1).
5. Стояки в помещении: Ст К1-1 Ø110, Ст В1-1 Ø32, Ст Т3-1 Ø32 — положение на плане выводов; выводы подключаются к ним по схеме разводки.
6. Ревизионные люки к арматуре и ревизиям в данных не заданы: место и размер не определены (записи реестра нет).
7. Помещение «Санузел 1 этажа» — 2 листа: стены 1) А, Б; 2) В, Г.
8. Расчёт систем водоснабжения и канализации и подбор оборудования выполняет проектная организация; лист задаёт места и высоты выводов.

1000 мм · печать 1:1

Изм.	Кол.уч	Лист	№ док.	Подп.	Дата
Разраб.		Кырлан А.С.			04.11.26
Пров.					
ГИП					
Н. контр.					
Утв.					

ГД-2026-010-АИ

Дом 331 м²

Общая площадь 270,67* м² · * размеры приняты, не замерены (реестр — л. 8–10, К-1)

Дизайн-проект интерьера

Стадия	Лист	Листов
РП	65	216

Развёртки мокрых зон: выводы ВК. Санузел 1 этажа (лист 2 из 2)

М 1:20

Кырлан Александр Сергеевич


выпуск 04.11.2026 № 2a77323a49 · стр. 67 из 221

Развёртки мокрых зон: выводы ВК. Санузел мастер (лист 1 из 2)


пом. 15 · выводы В1, Т3, К1 на стенах · высоты от чистого пола, привязки от чистовых углов, мм

ПРЕДВАРИТЕЛЬНО · не для производства работ · открыто пунктов: 15 (реестр — л. 8–10)

Стена А (М 1:20)

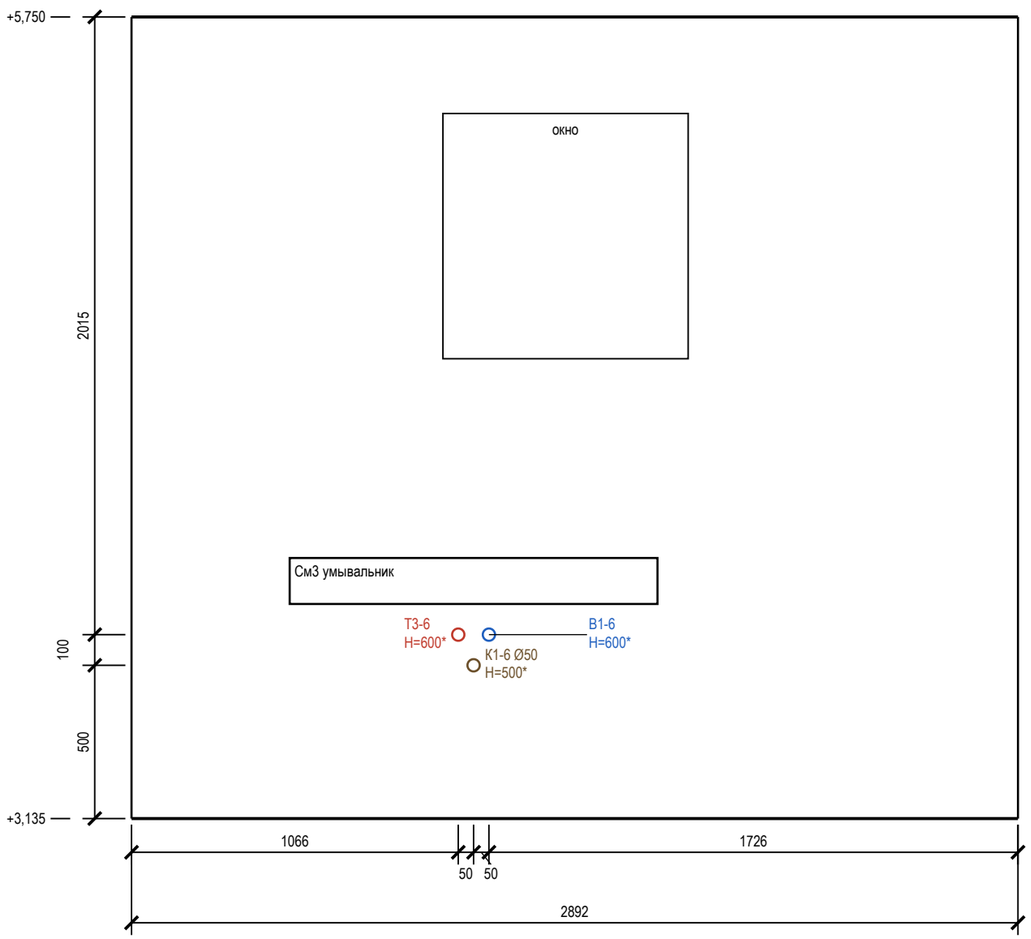

Стена Б (М 1:20)

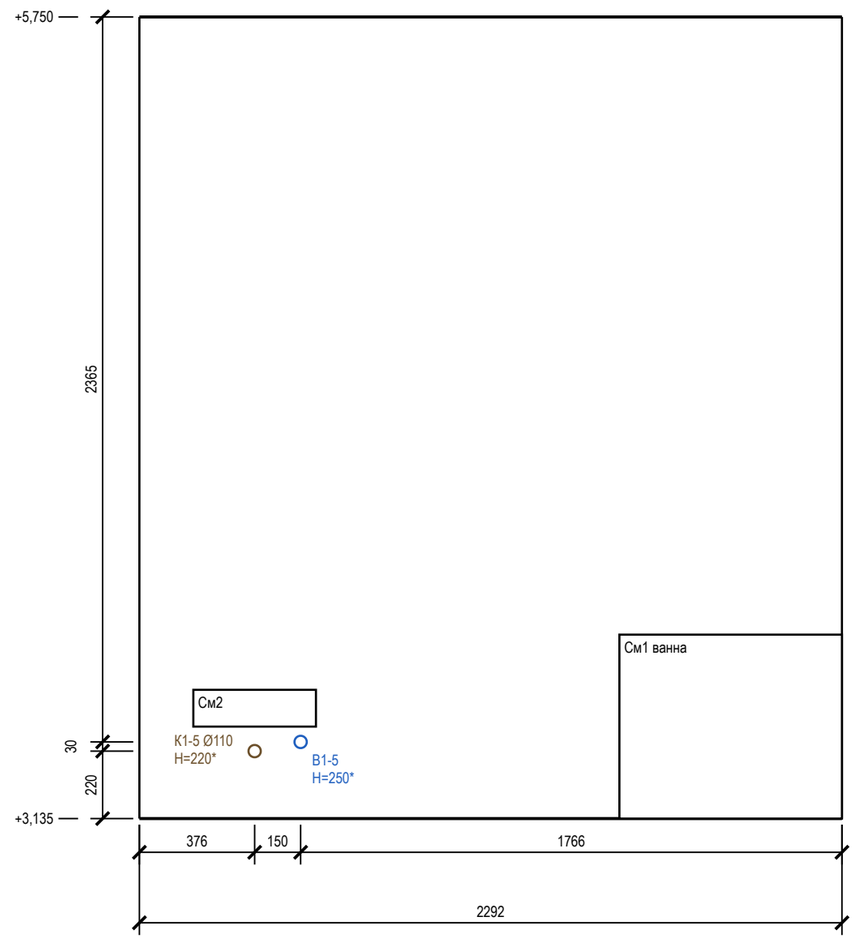

Допущения и предложения на листе

Основа листа: размеры и контуры этажей подобраны проектировщиком по составу помещений и площадям этажей с картинки 470 px (размеры на ней не читаются); обмер и исходный проект — задание (К-1); высоты: 1-й этаж 2800 мм, мансарда 2700 мм (горизонтальная часть) приняты; скаты кровли мансарды приняты по картинке: колено 1200 мм, уклон 45°, конёк вдоль длинной стороны; проект КР — задание (К-2); наружные стены 400 мм, перегородки 120 мм приняты (К-1); разрешённая мощность 15 кВт принята по типовым ТУ для частного дома (К-4); подрайон климата не задан — принят не северный (жилые от 2,5 м) (К-7).

См. лист открытых вопросов (лист 8, записи К-1, К-2, К-4, К-7).

Ведомость привязок выводов (от чистого пола и угла)

Код	Прибор	Ø	H, мм	Привязка, мм
В1-6	См3 умывальник	½"	600*	ст. А: 1166 от лев. угла
Т3-6	См3 умывальник	½"	600*	ст. А: 1066 от лев. угла
К1-6	См3 умывальник	Ø50	500*	ст. А: 1116 от лев. угла

Ведомость привязок (продолжение)

Код	Прибор	Ø	H, мм	Привязка, мм
В1-5	См2 унитаз подвесной	½"	250*	ст. Б: 526 от лев. угла
К1-5	См2 унитаз подвесной	Ø110	220*	ст. Б: 376 от лев. угла

Условные обозначения

- вывод В1 (код — в ведомости привязок)
- вывод Т3 (код — в ведомости привязок)
- вывод К1 (код — в ведомости привязок)
- сантехприбор по расстановке (габарит модели)
- дверной проём; окно — сплошной контур

Примечания

1. Габариты и высоты приборов, межосевые смесителей и места кранов — по паспортам выбранных приборов, сверяются до разметки стен.
2. Высоты Н — от чистого пола помещения, мм; отметка чистого пола и потолка — у левого края вида (от ±0,000 объекта). Привязки — от левого чистового угла вида (облицовка стен вычтена), как на развёртках стен.
3. * — высота принята по практике монтажа: в данных прибора её нет; до разметки стен сверить по паспорту выбранного прибора (смеситель, инсталляция, сифон).
4. Ревизионные люки к арматуре и ревизиям в данных не заданы: место и размер не определены (записи реестра нет).
5. Помещение «Санузел мастер» — 2 листа: стены 1) А, Б; 2) В, Г.
6. Расчёт систем водоснабжения и канализации и подбор оборудования выполняет проектная организация; лист задаёт места и высоты выводов.

1000 мм · печать 1:1

Изм.	Кол.уч	Лист	№ док.	Подп.	Дата
Разраб.		Кырлан А.С.			04.11.26
Пров.					
ГИП					
Н. контр.					
Утв.					

ГД-2026-010-АИ

Дом 331 м²

Общая площадь 270,67* м² · * размеры приняты, не замерены (реестр — л. 8–10, К-1)

Дизайн-проект интерьера

Стадия	Лист	Листов
РП	66	216

Развёртки мокрых зон: выводы ВК. Санузел мастер (лист 1 из 2)

М 1:20

Кырлан Александр Сергеевич


выпуск 04.11.2026 № 2a77323a49 · стр. 68 из 221

Развёртки мокрых зон: выводы ВК. Санузел мастер (лист 2 из 2)


пом. 15 · выводы В1, Т3, К1 на стенах · высоты от чистого пола, привязки от чистовых углов, мм

ПРЕДВАРИТЕЛЬНО · не для производства работ · открыто пунктов: 15 (реестр — л. 8–10)

Стена В (М 1:20)

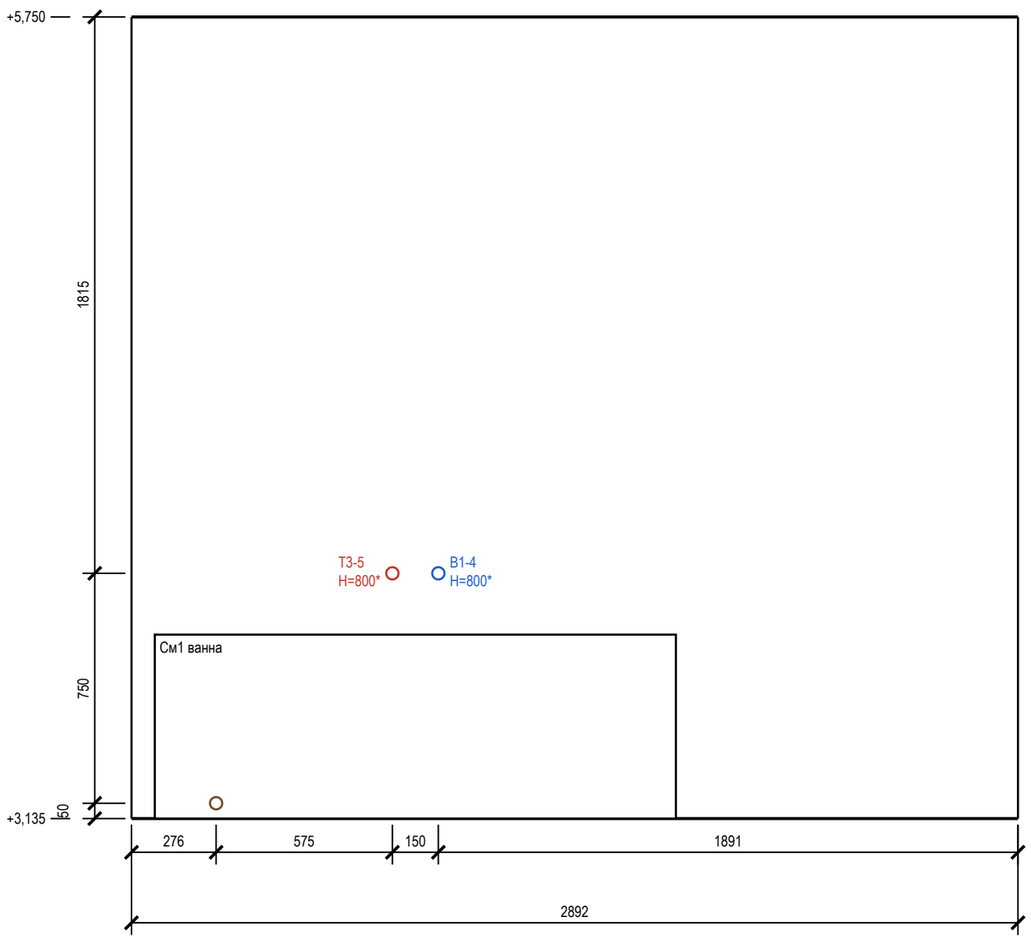

Стена Г (М 1:20)

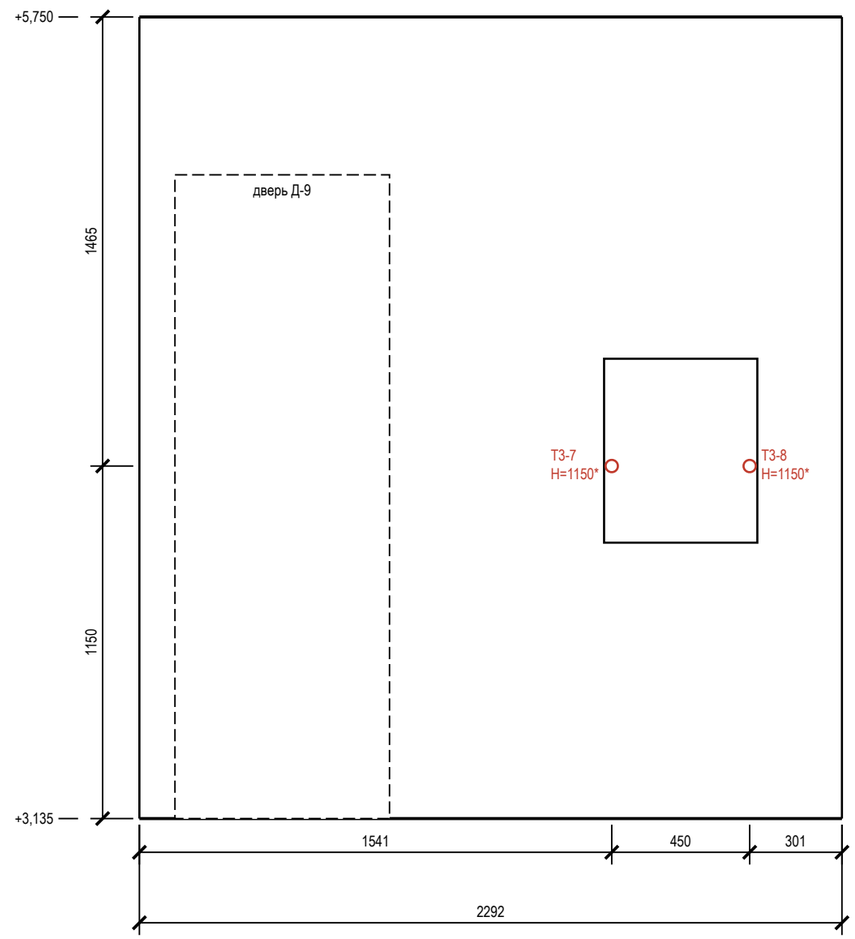

Допущения и предложения на листе

Основа листа: размеры и контуры этажей подобраны проектировщиком по составу помещений и площадям этажей с картинки 470 px (размеры на ней не читаются); обмер и исходный проект — задание (К-1); высоты: 1-й этаж 2800 мм, мансарда 2700 мм (горизонтальная часть) приняты; скаты кровли мансарды приняты по картинке: колено 1200 мм, уклон 45°, конёк вдоль длинной стороны; проект КР — задание (К-2); наружные стены 400 мм, перегородки 120 мм приняты (К-1); разрешённая мощность 15 кВт принята по типовым ТУ для частного дома (К-4); подрайон климата не задан — принят не северный (жилые от 2,5 м) (К-7).

См. лист открытых вопросов (лист 8, записи К-1, К-2, К-4, К-7).

Ведомость привязок выводов (от чистого пола и угла)

Код	Прибор	Ø	H, мм	Привязка, мм
В1-4	См1 ванна	½"	800*	ст. В: 1001 от лев. угла
Т3-5	См1 ванна	½"	800*	ст. В: 851 от лев. угла
К1-4	См1 ванна	Ø50	50*	ст. В: 276 от лев. угла

Ведомость привязок (продолжение)

Код	Прибор	Ø	H, мм	Привязка, мм
Т3-7	См4 полотенцесушитель	½"	1150*	ст. Г: 1541 от лев. угла
Т3-8	См4 полотенцесушитель	½"	1150*	ст. Г: 1991 от лев. угла

Условные обозначения

- вывод В1 (код — в ведомости привязок)
- вывод Т3 (код — в ведомости привязок)
- вывод К1 (код — в ведомости привязок)
- сантехприбор по расстановке (габарит модели)
- дверной проём; окно — сплошной контур

Примечания

1. Габариты и высоты приборов, межосевые смесителей и места кранов — по паспортам выбранных приборов, сверяются до разметки стен.
2. Высоты H — от чистого пола помещения, мм; отметка чистого пола и потолка — у левого края вида (от ±0,000 объекта). Привязки — от левого чистового угла вида (облицовка стен вычтена), как на развёртках стен.
3. * — высота принята по практике монтажа: в данных прибора её нет; до разметки стен сверить по паспорту выбранного прибора (смеситель, инсталляция, сифон).
4. Ревизионные люки к арматуре и ревизиям в данных не заданы: место и размер не определены (записи реестра нет).
5. Часть подписей выводов не уместилась у знака: коды и высоты — в ведомости привязок.
6. Помещение «Санузел мастер» — 2 листа: стены 1) А, Б; 2) В, Г.
7. Расчёт систем водоснабжения и канализации и подбор оборудования выполняет проектная организация; лист задаёт места и высоты выводов.

1000 мм · печать 1:1

Изм.	Кол.уч	Лист	№ док.	Подп.	Дата
Разраб.		Кырлан А.С.			04.11.26
Пров.					
ГИП					
Н. контр.					
Утв.					

ГД-2026-010-АИ

Дом 331 м²

Общая площадь 270,67* м² · * размеры приняты, не замерены (реестр — л. 8–10, К-1)

Дизайн-проект интерьера

Стадия	Лист	Листов
РП	67	216

Развёртки мокрых зон: выводы ВК. Санузел мастер (лист 2 из 2)

М 1:20


Кырлан Александр Сергеевич

выпуск 04.11.2026 № 2a77323a49 · стр. 69 из 221


Развёртки мокрых зон: выводы ВК. Санузел 2 (лист 1 из 2)

пом. 20 · выводы В1, Т3, К1 на стенах · высоты от чистого пола, привязки от чистовых углов, мм

Стена А (М 1:20)

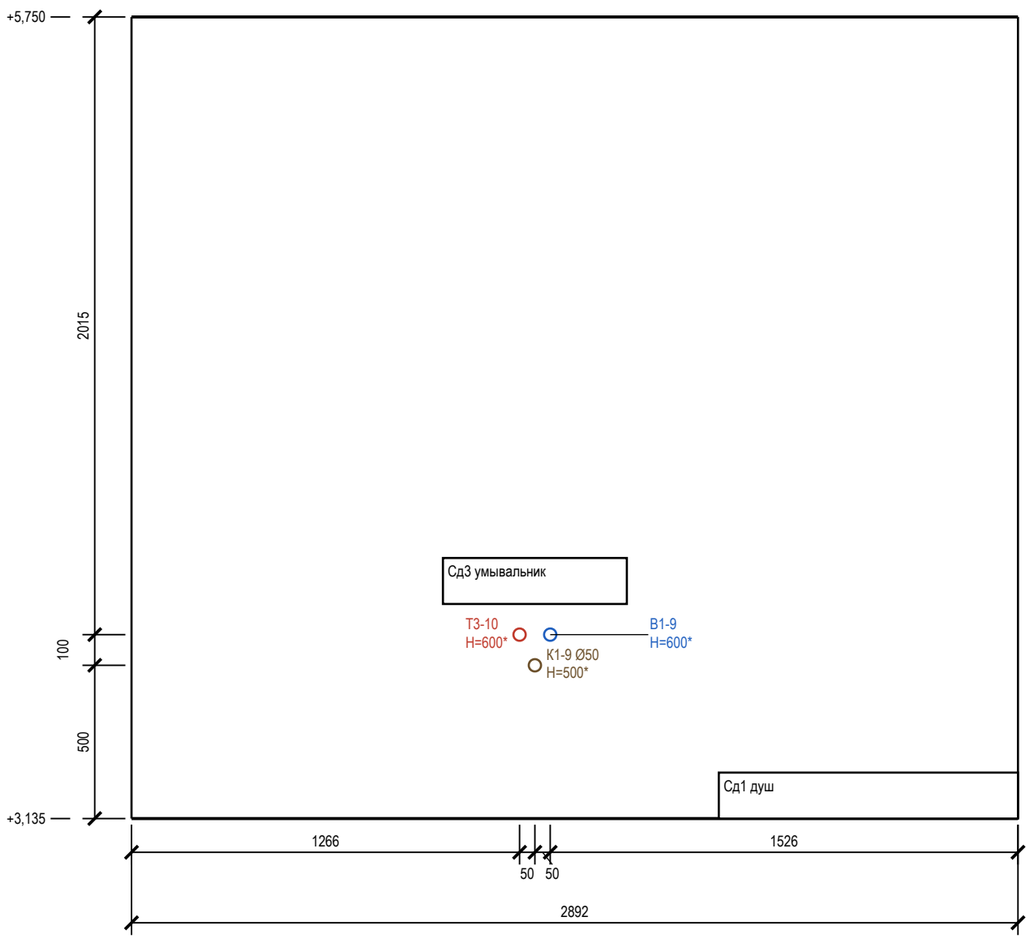

Стена Б (М 1:20)

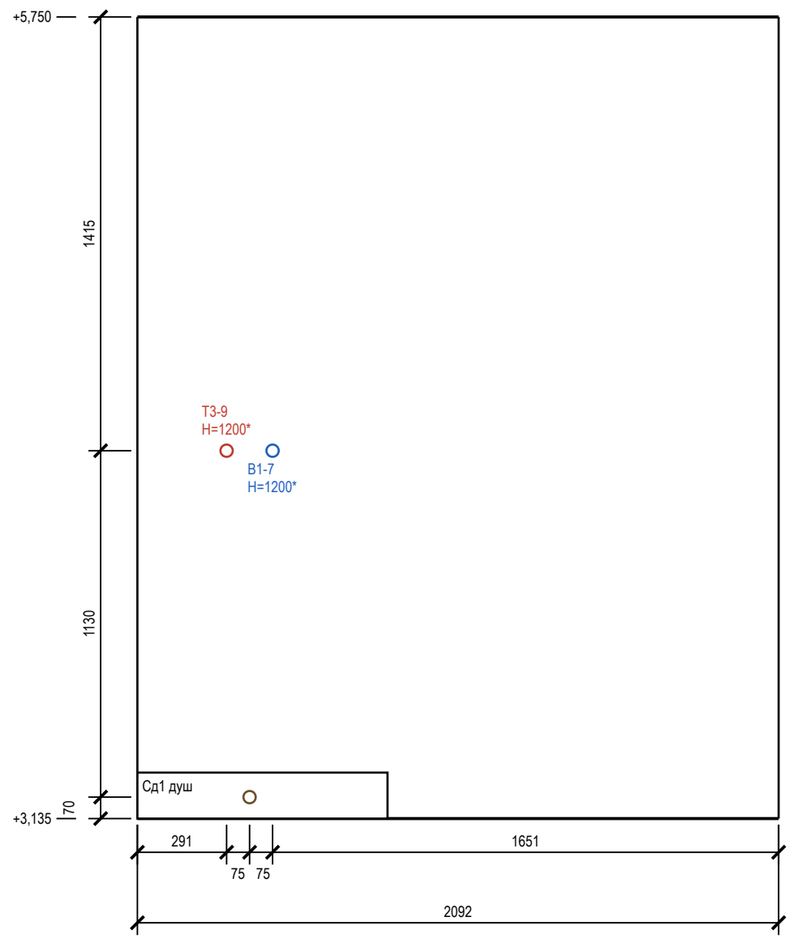

Допущения и предложения на листе

Основа листа: размеры и контуры этажей подобраны проектировщиком по составу помещений и площадям этажей с картинки 470 px (размеры на ней не читаются); обмер и исходный проект — задание (К-1); высоты: 1-й этаж 2800 мм, мансарда 2700 мм (горизонтальная часть) приняты; скаты кровли мансарды приняты по картинке: колено 1200 мм, уклон 45°, конёк вдоль длинной стороны; проект КР — задание (К-2); наружные стены 400 мм, перегородки 120 мм приняты (К-1); разрешённая мощность 15 кВт принята по типовым ТУ для частного дома (К-4); подрайон климата не задан — принят не северный (жилые от 2,5 м) (К-7).

См. лист открытых вопросов (лист 8, записи К-1, К-2, К-4, К-7).

Ведомость привязок выводов (от чистого пола и угла)

Код	Прибор	Ø	H, мм	Привязка, мм
В1-9	Сд3 умывальник	½"	600*	ст. А: 1366 от лев. угла
Т3-10	Сд3 умывальник	½"	600*	ст. А: 1266 от лев. угла
К1-9	Сд3 умывальник	Ø50	500*	ст. А: 1316 от лев. угла

Ведомость привязок (продолжение)

Код	Прибор	Ø	H, мм	Привязка, мм
В1-7	Сд1 душ	½"	1200*	ст. Б: 441 от лев. угла
Т3-9	Сд1 душ	½"	1200*	ст. Б: 291 от лев. угла
К1-7	Сд1 душ	Ø50	70*	ст. Б: 366 от лев. угла

Условные обозначения

- вывод В1 (код — в ведомости привязок)
- вывод Т3 (код — в ведомости привязок)
- вывод К1 (код — в ведомости привязок)
- сантехприбор по расстановке (габарит модели)
- дверной проём; окно — сплошной контур

Примечания

1. Габариты и высоты приборов, межосевые смесителей и места кранов — по паспортам выбранных приборов, сверяются до разметки стен.
2. Высоты H — от чистого пола помещения, мм; отметка чистого пола и потолка — у левого края вида (от ±0,000 объекта). Привязки — от левого чистового угла вида (облицовка стен вычтена), как на развёртках стен.
3. * — высота принята по практике монтажа: в данных прибора её нет; до разметки стен сверить по паспорту выбранного прибора (смеситель, инсталляция, сифон).
4. Стояки в помещении: Ст К1-3 Ø110, Ст В1-3 Ø32, Ст Т3-3 Ø32 — положение на плане выводов; выводы подключаются к ним по схеме разводки.
5. Ревизионные люки к арматуре и ревизиям в данных не заданы: место и размер не определены (записи реестра нет).
6. Часть подписей выводов не уместилась у знака: коды и высоты — в ведомости привязок.
7. Помещение «Санузел 2» — 2 листа: стены 1) А, Б; 2) В.
8. Расчёт систем водоснабжения и канализации и подбор оборудования выполняет проектная организация; лист задаёт места и высоты выводов.

1000 мм · печать 1:1

Изм.	Кол.уч	Лист	№ док.	Подп.	Дата
Разраб.		Кырлан А.С.			04.11.26
Пров.					
ГИП					
Н. контр.					
Утв.					

ГД-2026-010-АИ

Дом 331 м²

Общая площадь 270,67* м² · * размеры приняты, не замерены (реестр — л. 8–10, К-1)

Дизайн-проект интерьера

Стадия	Лист	Листов
РП	68	216

Развёртки мокрых зон: выводы ВК. Санузел 2 (лист 1 из 2)

М 1:20

Кырлан Александр Сергеевич


выпуск 04.11.2026 № 2a77323a49 · стр. 70 из 221

Развёртки мокрых зон: выводы ВК. Санузел 2 (лист 2 из 2)

пом. 20 · выводы B1, T3, K1 на стенах · высоты от чистого пола, привязки от чистовых углов, мм

ПРЕДВАРИТЕЛЬНО · не для производства работ · открыто пунктов: 15 (реестр — л. 8–10)

Стена В (М 1:20)

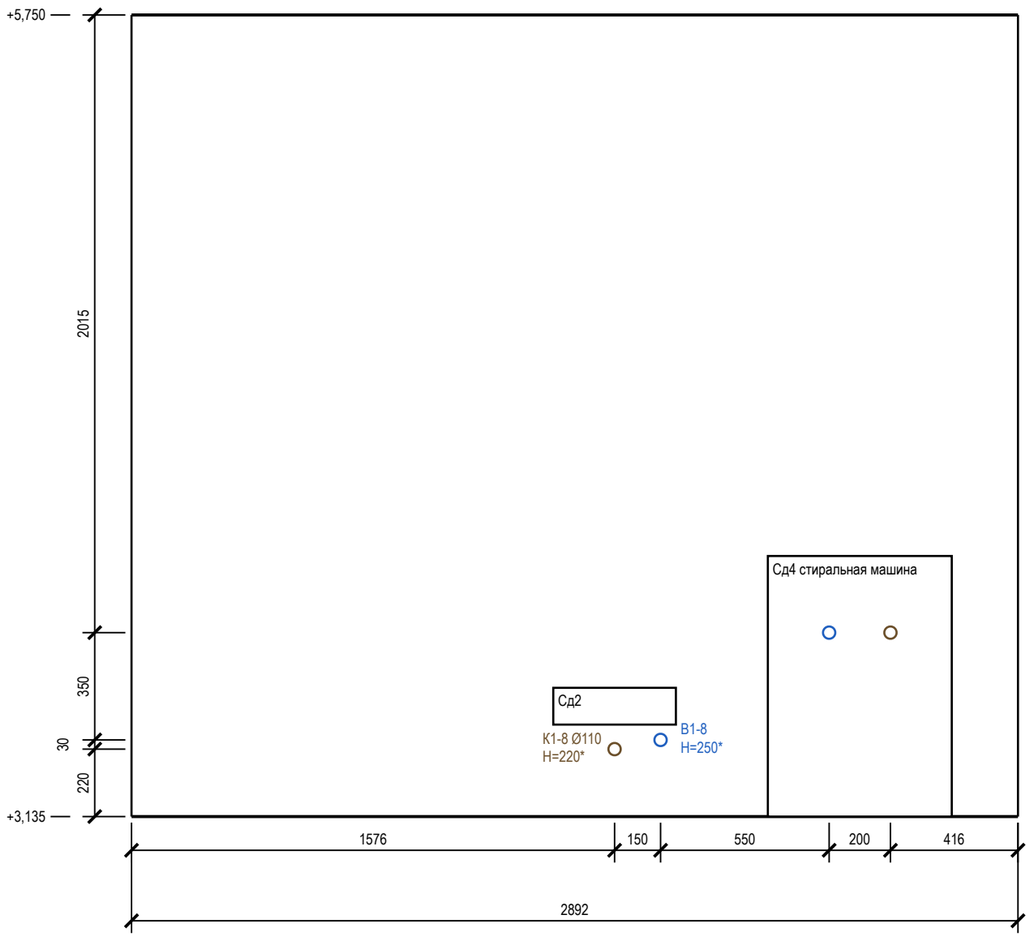

Допущения и предложения на листе

Основа листа: размеры и контуры этажей подобраны проектировщиком по составу помещений и площадям этажей с картинки 470 px (размеры на ней не читаются); обмер и исходный проект — задание (К-1); высоты: 1-й этаж 2800 мм, мансарда 2700 мм (горизонтальная часть) приняты; скаты кровли мансарды приняты по картинке: колено 1200 мм, уклон 45°, конёк вдоль длинной стороны; проект КР — задание (К-2); наружные стены 400 мм, перегородки 120 мм приняты (К-1); разрешённая мощность 15 кВт принята по типовым ТУ для частного дома (К-4); подрайон климата не задан — принят не северный (жилые от 2,5 м) (К-7).

См. лист открытых вопросов (лист 8, записи К-1, К-2, К-4, К-7).

Ведомость привязок выводов (от чистого пола и угла)

Код	Прибор	Ø	H, мм	Привязка, мм
B1-8	Сд2 унитаз подвесной	½"	250*	ст. В: 1726 от лев. угла
K1-8	Сд2 унитаз подвесной	Ø110	220*	ст. В: 1576 от лев. угла

Ведомость привязок (продолжение)

Код	Прибор	Ø	H, мм	Привязка, мм
B1-10	Сд4 стиральная машина	½"	600*	ст. В: 2276 от лев. угла
K1-10	Сд4 стиральная машина	Ø50	600*	ст. В: 2476 от лев. угла

Условные обозначения

- вывод B1 (код — в ведомости привязок)
- вывод T3 (код — в ведомости привязок)
- вывод K1 (код — в ведомости привязок)
- сантехприбор по расстановке (габарит модели)
- дверной проём; окно — сплошной контур

Примечания

1. Габариты и высоты приборов, межосевые смесители и места кранов — по паспортам выбранных приборов, сверяются до разметки стен.
2. Высоты H — от чистого пола помещения, мм; отметка чистого пола и потолка — у левого края вида (от ±0,000 объекта). Привязки — от левого чистового угла вида (облицовка стен вычтена), как на развёртках стен.
3. * — высота принята по практике монтажа: в данных прибора её нет; до разметки стен сверить по паспорту выбранного прибора (смеситель, инсталляция, сифон).
4. Стояки в помещении: Ст К1-3 Ø110, Ст В1-3 Ø32, Ст Т3-3 Ø32 — положение на плане выводов; выводы подключаются к ним по схеме разводки.
5. Ревизионные люки к арматуре и ревизиям в данных не заданы: место и размер не определены (записи реестра нет).
6. Часть подписей выводов не уместилась у знака: коды и высоты — в ведомости привязок.
7. Помещение «Санузел 2» — 2 листа: стены 1) А, Б; 2) В.
8. Расчёт систем водоснабжения и канализации и подбор оборудования выполняет проектная организация; лист задаёт места и высоты выводов.

1000 мм · печать 1:1

Изм.	Кол.уч	Лист	№ док.	Подп.	Дата
Разраб.		Кырлан А.С.			04.11.26
Пров.					
ГИП					
Н. контр.					
Утв.					

ГД-2026-010-АИ

Дом 331 м²

Общая площадь 270,67* м² · * размеры приняты, не замерены (реестр — л. 8–10, К-1)

Дизайн-проект интерьера

Стадия	Лист	Листов
РП	69	216

Развёртки мокрых зон: выводы ВК. Санузел 2 (лист 2 из 2)

М 1:20

Кырлан Александр Сергеевич

выпуск 04.11.2026 № 2a77323a49 · стр. 71 из 221

Спецификация сантехнического оборудования

Форма 1 ГОСТ 21.110-2013 · ГД-2026-010-АИ-ВК.СО · приборы, арматура, трубопроводы

ПРЕДВАРИТЕЛЬНО · не для производства работ · открыто пунктов: 15 (реестр — л. 8–10)

Поз.	Наименование и техническая характеристика	Тип, марка, обозначение документа	Код продукции	Поставщик	Ед. изм.	Кол.	Масса 1 ед., кг	Примечание
	Санитарные приборы							
1	Ванна встраиваемая акриловая 1700×750 мм, с каркасом, экраном и отверстием слив-перелив	аналог		выбор заказчика	шт	1		См1
2	Унитаз подвесной безободковый, с сиденьем микролифт, крепёж и звукоизолирующая прокладка	Jacob Delafon Struktura EDF102-00		выбор заказчика	шт	3		Сн2, См2, Сд2
3	Инсталляция для подвесного унитаза: рама высотой 1120 мм, бачок, клавиша смыва (ось клавиши 1050 мм от чистого пола)	аналог		выбор заказчика	шт	3		Сн2, См2, Сд2; короб ГКЛВ
4	Раковина накладная 700×500 мм, на столешницу тумбы, с переливом	аналог		выбор заказчика	шт	1		Сн3
5	Раковина накладная 1200×500 мм, на столешницу тумбы, с переливом	аналог		выбор заказчика	шт	1		См3
6	Умывальник подвесной 600×450 мм, с отверстием под смеситель и переливом	аналог		выбор заказчика	шт	1		Сд3
7	Поддон душевой низкий 900×1000 мм, с сифоном и выпуском Ø50, на ножках/подиуме	аналог		выбор заказчика	шт	1		Сд1
8	Трап душевой с гидрозатвором и фланцем под гидроизоляцию, монтажная высота по паспорту	аналог		выбор заказчика	шт	1		Сн1**; узел 1 схема разводки
9	Мойка кухонная врезная / подстольная, с переливом, ориентир 700×480 мм — в модуле Кх1 шириной 800 мм, вырез по шаблону модели	аналог		с кухонной мебелью	шт	1		Кх1
10	Полотенцесушитель водяной (ГВС), с байпасом и кранами	аналог		выбор заказчика	шт	2		Сн4, См4
	Смесители, сифоны и арматура приборов							
11	Смеситель для ванны настенный однорычажный, межосевое 150 мм, с душевым набором (лейка, шланг, держатель)	аналог		выбор заказчика	шт	1		См1
12	Смеситель для накладной раковины однорычажный, высокий излив, с донным клапаном	аналог		выбор заказчика	шт	2		Сн3, См3
13	Смеситель для умывальника однорычажный, с донным клапаном	аналог		выбор заказчика	шт	1		Сд3
14	Душевая система скрытого монтажа с термостатом: встраиваемая часть, верхний душ, ручная лейка	аналог		выбор заказчика	шт	2		Сн1**, Сд1; встраиваемая часть — до плитки
15	Смеситель кухонный однорычажный, высокий излив	аналог		выбор заказчика	шт	1		Кх1
16	Обвязка ванны слив-перелив Ø40/50 с сифоном	аналог		выбор заказчика	шт	1		См1
17	Сифон для умывальника бутылочный Ø32/40–50, с гофрой к выпуску	аналог		выбор заказчика	шт	3		Сн3, См3, Сд3
18	Сифон для мойки Ø40/50	аналог		выбор заказчика	шт	1		Кх1
19	Сифон для посудомоечной машины с обратным клапаном, на выводе слива Ø40	аналог		выбор заказчика	шт	1		Кх2
20	Сифон для стиральной машины встраиваемый в стену Ø50, с обратным клапаном	аналог		выбор заказчика	шт	1		Сд4
21	Кран угловой ½"×½" с гибкой подводкой 40 см (умывальники, мойка)	аналог		выбор заказчика	шт	8		по 2 на прибор
22	Кран шаровой угловой ½"×¾" для подключения стиральной и посудомоечной машины	аналог		выбор заказчика	шт	2		Сд4, Кх2
23	Узел подключения полотенцесушителя: байпас Ду20, краны шаровые ½" ×2	аналог		выбор заказчика	шт	2		
	Трубопроводы							
24	Труба полипропиленовая PP-R PN20 Ø20×3,4 (В1)	ГОСТ 32415-2013		выбор заказчика	м	32,5	0,17	21,5 + 7,6 + 10 %
25	Труба PP-R, армированная стекловолокном, PN20 Ø20×2,8 (Т3)	ГОСТ 32415-2013		выбор заказчика	м	39,5	0,15	25,2 + 10,3 + 10 %
26	Труба канализационная ПП Ø40 (К1)	ГОСТ 32414-2013		выбор заказчика	м	1		0,1 + 0,6 + 10 %
27	Труба канализационная ПП Ø50 (К1)	ГОСТ 32414-2013		выбор заказчика	м	17,5		13,1 + 2,7 + 10 %
28	Труба канализационная ПП Ø110 (К1)	ГОСТ 32414-2013		выбор заказчика	м	8,5		6,7 + 0,7 + 10 %
	Фасонные части и выводы							
29	Отвод канализационный ПП 45° Ø50	ГОСТ 32414-2013		выбор заказчика	шт	22		2 шт. на поворот
30	Отвод канализационный ПП 45° Ø110	ГОСТ 32414-2013		выбор заказчика	шт	16		2 шт. на поворот
31	Тройник канализационный ПП 45° (врезки ветвей)	ГОСТ 32414-2013		выбор заказчика	шт	11		
32	Ревизия канализационная ПП (после поворота трассы)	ГОСТ 32414-2013		выбор заказчика	шт	10		доступ сохранить
33	Фитинги PP-R Ø20: тройники, угольники 90° (ветви и повороты В1, Т3)	ГОСТ 32415-2013		выбор заказчика	шт	55		
34	Водорозетка PP-R Ø20×½" настенная, с креплением	ГОСТ 32415-2013		выбор заказчика	шт	23		коды — лист выводов
	Узлы ввода, люки, короба							
35	Кран шаровой латунный Ду15 PN16 (отключение ввода)	аналог		выбор заказчика	шт	6		Ст В1-1, Ст Т3-1, Ст В1-2, Ст Т3-2, Ст В1-3, Ст Т3-3
36	Фильтр сетчатый косой Ду15	аналог		выбор заказчика	шт	6		
37	Счётчик воды крыльчатый Ду15 (ХВ, ГВ), с поверкой	аналог		выбор заказчика	шт	6		пломба УК
38	Клапан обратный Ду15	аналог		выбор заказчика	шт	6		
39	Люк ревизионный нажимной под плитку 300×400 мм	аналог		выбор заказчика	шт	3		к стоякам и арматуре
40	Звукоизоляция стояка К1 в коробе: рулонный звукоизоляционный материал ≥ 10 мм, обмотка стояка на высоту этажа	аналог		выбор заказчика	м	8,4		Ст К1-1, Ст К1-2 (кухня), Ст К1-3
41	Короб К1 над полом: профиль ПН/ПС, ГКЛВ 12,5 мм под плитку	аналог		выбор заказчика	м	14,6		сечение — лист разводки

Примечания

1. Форма 1 ГОСТ 21.110-2013, ширины граф изменены по п. 4.1. «Аналог» — аналог по характеристикам: модели внести до черновых работ, привязки выводов сверить по паспортам.
2. Бытовая техника не входит (показана арматура подключения), мойка — в комплекте кухни (марка — модуля кухни, как у столяра). Длины труб — трасса листа разводки + подъёмы + 10 %.
3. Стояк К1 в коробе — звукоизоляция стояка в коробе без жёсткого контакта короба с трубой.
4. Расчёт систем водоснабжения и канализации, диаметры магистралей и подбор оборудования выполняет проектная организация.

Допущения и предложения на листе

Основа листа: размеры и контуры этажей подобраны проектировщиком по составу помещений и площадям этажей с картинки 470 px (размеры на ней не читаются); обмер и исходный проект — задание (К-1); высоты: 1-й этаж 2800 мм, мансарда 2700 мм (горизонтальная часть) приняты; скаты кровли мансарды приняты по картинке: колено 1200 мм, уклон 45°, конёк вдоль длинной стороны; проект КР — задание (К-2); наружные стены 400 мм, перегородки 120 мм приняты (К-1); разрешённая мощность 15 кВт принята по типовым ТУ для частного дома (К-4); подрайон климата не задан — принят не северный (жилые от 2,5 м) (К-7).

Знак «**» — предложение проектировщика, заказчиком не утверждено (согласовать с заказчиком): К-8: Сн1 — Подиум душевой зоны 100 мм — предложение проектировщика: трап в стяжке 35 мм не встаёт (монтажная высота трапа 90 + уклон отвода до стояка 42 = 132 мм).

См. лист открытых вопросов (лист 8, записи К-1, К-2, К-4, К-7; лист 9, запись К-8).

Изм.	Кол.уч	Лист	№ док.	Подп.	Дата
Разраб.		Кырлан А.С.			04.11.26
Пров.					
ГИП					
Н. контр.					
Утв.					

ГД-2026-010-АИ

Дом 331 м²

Общая площадь 270,67* м² · * размеры приняты, не замерены (реестр — л. 8–10, К-1)

Дизайн-проект интерьера

Стадия	Лист	Листов
РП	70	216

Спецификация сантехнического оборудования

М б/м

Кырлан Александр Сергеевич

выпуск 04.11.2026 № 2a77323a49 · стр. 72 из 221

Техническое задание на подбор светильников

ПРЕДВАРИТЕЛЬНО · не для производства работ · открыто пунктов: 15 (реестр — л. 8–10)

Параметры для подбора: светильники, ленты и блоки питания, сценарии помещений со светорегуляторами · б/м

Параметры светильников для подбора

Поз.	Марки	Наименование	Установка	Кол.	P, Вт	Σ P, Вт	Ф, лм	Тц, К	Ra	Угол, °	IP	Дим.	Слой	Группа	Пом.
1	Св1–Св8, Св31–Св37	Встраиваемый точечный	в ГКЛ, корпус ≤ 70 мм	15	12	180	1000	3000	90	—	20	—	общий	L1, L4	1, 5
2	Св38, Св39	Линейный светильник	на поверхности	1,2 м	8	16	700	3000	90	—	20	—	рабочий	L5	1
3	Св40	Лента светодиодная 24 В	в нише уровня, профиль с рассеивателем	10,2 м	9,6/м	97,8	900/м	2700	90	—	20	да	акцентный	L6	1
4	Св17–Св22, Св76–Св81, Св87–Св92, Св96–Св101	Встраиваемый точечный	в ГКЛ, корпус ≤ 70 мм	24	12	288	1050	2700	90	—	20	—	общий	L7	2, 16, 18, 19
5	Св23	Лента светодиодная 24 В	в нише уровня, профиль с рассеивателем	5,4 м	9,6/м	51,9	900/м	2700	90	—	20	да	акцентный	L8	2
6	Св11, Св24, Св25, Св70, Св83, Св84, Св94, Св95, Св103, Св104	Настенный (бра)	на стене, H=1500	10	6	60	400	2700	90	60	20	да	рабочий	L3, L9	2, 13, 16, 18, 19
7	Св12–Св14, Св51, Св72–Св74	Встраиваемый точечный	в ГКЛ, корпус ≤ 70 мм	7	6	42	500	3000	90	—	44	—	общий	L4, L17	3, 15, 20
8	Св15**, Св52**, Св75**	Настенный светильник над зеркалом, драйвер встроен	над зеркалом, H=1900	3	8	24	600	3000	90	—	44	—	рабочий	L5, L18	3, 15, 20
9	Св16, Св55, Св58, Св71	Потолочный накладной	на потолке	4	10	40	900	3000	90	—	20	—	общий	L6, L19, L21	4, 7, 9, 14
10	Св9	Подвесной	подвес, низ H=1600	1	15	15	1200	2700	90	—	20	—	рабочий	L2	5
11	Св10	Лента светодиодная 24 В	в карнизе короба, профиль с рассеивателем	21,1 м	9,6/м	202,9	900/м	2700	90	—	20	да	акцентный	L3	5
12	Св26–Св29, Св53, Св54, Св85, Св86	Встраиваемый точечный	в ГКЛ, корпус ≤ 70 мм	8	7	56	600	3000	90	—	20	—	общий	L10	6, 8, 17
13	Св30**	Лента светодиодная 24 В	на поверхности, профиль с рассеивателем, датчик движения	1,8 м	4,8/м	8,6	150/м	2700	90	—	20	нет	ночной	L11	8
14	Св56, Св57	Потолочный накладной	на потолке	2	24	48	2500	3000	90	—	20	—	общий	L20	10
15	Св59**, Св60**	Накладной точечный светильник (downlight)	на потолке	2	9	18	800	3000	90	—	44	—	общий	L12, L13	11, 12
16	Св61–Св68	Встраиваемый точечный	в ГКЛ, корпус ≤ 70 мм	8	12	96	1000	2700	90	—	20	—	общий	L1	13
17	Св69, Св102	Лента светодиодная 24 В	в карнизе короба, профиль с рассеивателем	12 м	9,6/м	115,2	900/м	2700	90	—	20	да	акцентный	L2, L8	13, 19
18	Св82	Лента светодиодная 24 В	в нише уровня, профиль с рассеивателем	3,2 м	9,6/м	30,4	900/м	2700	90	—	20	да	акцентный	L8	16
19	Св93	Лента светодиодная 24 В	в карнизе короба, профиль с рассеивателем	15,5 м	9,6/м	149,2	900/м	2700	90	—	20	да	акцентный	L8	18
20	Св50	Встраиваемый точечный	в ГКЛ, корпус ≤ 70 мм	1	7	7	600	3000	90	—	44	—	общий	L17	20
		Итого		**85 шт + 70,4 м**		**1546,2**									

LED-ленты, линейные светильники и блоки питания

Марка	Пом.	L, м	U, В	Вт/м	Σ P, Вт	БП	P БП, Вт	Загр., %	Питание	Доступ к БП
Св38	1	0,6	24	—	8	БП2	30	53	встроенный ввод	в навесном модуле Кх11, съёмная панель
Св39	1	0,6	24	—	8	БП2	30	53	встроенный ввод	в навесном модуле Кх11, съёмная панель
Св40	1	10,2	24	9,6	97,8	БП3	150	65	с двух концов	люк 300×300 в нише фигуры потолка ПТ1
Св23	2	5,4	24	9,6	51,9	БП4	200	26	с двух концов	люк 300×300 в нише фигуры потолка ПТ2
Св10	5	21,1	24	9,6	202,9	БП1	300	68	с двух концов	люк 300×300 в коробе потолка ПТ2
Св30**	8	1,8	24	4,8	8,6	БП5	20	43	с одного конца	в шкафу Пх1, верхняя полка
Св69	13	6	24	9,6	57,6	БП6	200	29	с двух концов	люк 300×300 в коробе потолка ПТ5
Св82	16	3,2	24	9,6	30,4	БП7	200	15	с двух концов	люк 300×300 в нише фигуры потолка ПТ5
Св93	18	15,5	24	9,6	149,2	БП8	200	75	с двух концов	люк 300×300 в коробе потолка ПТ5
Св102	19	6	24	9,6	57,6	БП9	200	29	с двух концов	люк 300×300 в коробе потолка ПТ5

Сценарии (помещения со светорегуляторами)

Помещение	Сценарий	Горят группы (уровень)	Управление
5. Гостиная	Вечер	L2 подвес над обеденным столом — вкл.; L3 лента в карнизе (диммер) — 50 %; остальные выкл.	светорегулятор S2**; выключатель S1
	Гости	L1 общий свет (споты) — вкл.; L2 подвес над обеденным столом — вкл.; L3 лента в карнизе (диммер) — 100 %	светорегулятор S2**; выключатель S1
	Кино	L3 лента в карнизе (диммер) — 20 %; остальные выкл.	светорегулятор S2**
	Уборка	L1 общий свет (споты) — вкл.; L2 подвес над обеденным столом — вкл.; остальные выкл.	выключатель S1
13. Спальня мастер	Вечер	L2 подсветка короба — вкл.; L3 бра — 100 %; остальные выкл.	выключатели S3, S21, S22
	Уборка	L1 споты — вкл.; L2 подсветка короба — вкл.; остальные выкл.	выключатели S3, S21, S22

Примечания

1. Позиции и марки Св — те же, что на плане освещения (листы 39, 40) и в ведомости светильников (лист 43); группы L — по плану выключателей (листы 41, 42).
2. Модели светильников не выбраны: лист — техническое задание на подбор. Модель по строке таблицы: поток, Тц, Ra, угол, IP и регулировка яркости не хуже указанных, мощность не больше; встраиваемые — под глубину короба (графа «Установка»). IP 20 — сухие помещения. После выбора моделей (артикул, производитель) лист выпускается как «Спецификация светильников».
3. Длина LED-ленты в карнизе и нише уровня — по линиям карниза и ниши плана потолков (листы 73, 74); Σ P = Вт/м × длина. Блок питания загружен не больше чем на 80 %; лента 24 В длиннее 10 м питается с двух концов; доступ к блоку питания — люк ревизии 300×300 мм или место, указанное в таблице.
4. Сценарии: % — яркость группы на светорегуляторе; «вкл.» — группа на обычной клавише; группы, не названные в строке, выключены. Светильники и блоки питания групп на светорегуляторе — с регулировкой яркости. Клавиши и светорегуляторы — листы 41, 42.
5. В пом. 2, 16, 18, 19 свет включается клавишами групп — листы 41, 42.
6. Мощность и поток в таблице — требования к подбору (поток не меньше, мощность не больше указанных); после выбора модели — по её паспорту, Σ P — установленная мощность освещения. Оценка освещённости — на плане освещения; это не светотехнический расчёт.
7. Окончание: «Слои света по помещениям» — лист 72.

Допущения и предложения на листе. Знак «**» предложено (согласовать). См. лист открытых вопросов (листы 8–10).

Изм.	Кол.уч	Лист	№ док.	Подп.	Дата
Разраб.		Кырлан А.С.			04.11.26
Пров.					
ГИП					
Н. контр.					
Утв.					

ГД-2026-010-АИ

Дом 331 м²

Общая площадь 270,67* м² · * размеры приняты, не замерены (реестр — л. 8–10, К-1)

Дизайн-проект интерьера	Стадия	Лист	Листов
	РП	71	216

Техническое задание на подбор светильников

М б/м

Кырлан Александр Сергеевич

выпуск 04.11.2026 № 2a77323a49 · стр. 73 из 221

Техническое задание на подбор светильников (продолжение)

Продолжение таблиц · б/м

Слои света по помещениям

Пом.	Помещение	Слои света — группы включения (марки — в спецификации)	Σ P, Вт
1	Кухня-столовая	общий — L4; рабочий — L5; акцентный — L6	197,8
2	Кабинет-гостевая	общий — L7; рабочий — L9; акцентный — L8	135,9
3	Санузел 1 этажа	общий — L4; рабочий — L5	26
4	Котельная	общий — L21	10
5	Гостиная	общий — L1; рабочий — L2; акцентный — L3	313,9
6	Холл с лестницей	общий — L10	14
7	Кладовая	общий — L6	10
8	Прихожая	общий — L10; ночной — L11	36,6
9	Тамбур	общий — L19	10
10	Гараж	общий — L20	48
11	Веранда	общий — L12	9
12	Крыльцо	общий — L13	9
13	Спальня мастер	общий — L1; рабочий — L3; акцентный — L2	165,6
14	Гардеробная мастер	общий — L6	10
15	Санузел мастер	общий — L4; рабочий — L5	26
16	Спальня 2	общий — L7; рабочий — L9; акцентный — L8	114,4
17	Холл мансарды	общий — L10	14
18	Спальня 3	общий — L7; рабочий — L9; акцентный — L8	233,2
19	Спальня 4	общий — L7; рабочий — L9; акцентный — L8	141,6
20	Санузел 2	общий — L17; рабочий — L18	21

Слои света

общий — равномерный свет помещения, по норме освещённости

рабочий — местный свет задачи: столешница, зеркало, чтение у кровати

акцентный — подсветка потолка, стен и ниш; не входит в поток общего света

ночной — путь спальня → санузел: не выше 2700 K, малая яркость, датчик движения

Примечания

1. Продолжение листа 71: позиции, марки и группы — те же, что на основном листе.
2. Σ P — установленная мощность освещения помещения, Вт; группы L — по плану выключателей.

Допущения и предложения на листе

Основа листа: размеры и контуры этажей подобраны проектировщиком по составу помещений и площадям этажей с картинки 470 px (размеры на ней не читаются); обмер и исходный проект — задание (К-1); высоты: 1-й этаж 2800 мм, мансарда 2700 мм (горизонтальная часть) приняты; скаты кровли мансарды приняты по картинке: колено 1200 мм, уклон 45°, конёк вдоль длинной стороны; проект КР — задание (К-2); наружные стены 400 мм, перегородки 120 мм приняты (К-1); разрешённая мощность 15 кВт принята по типовым ТУ для частного дома (К-4); подрайон климата не задан — принят не северный (жилые от 2,5 м) (К-7).

См. лист открытых вопросов (лист 8, записи К-1, К-2, К-4, К-7).

Изм.	Кол.уч	Лист	№ док.	Подп.	Дата
Разраб.		Кырлан А.С.			04.11.26
Пров.					
ГИП					
Н. контр.					
Утв.					

ГД-2026-010-АИ

Дом 331 м²

Общая площадь 270,67* м² · * размеры приняты, не замерены (реестр — л. 8–10, К-1)

Дизайн-проект интерьера

Стадия	Лист	Листов
РП	72	216

Техническое задание на подбор светильников (продолжение)

М б/м


Кырлан Александр Сергеевич

выпуск 04.11.2026 № 2a77323a49 · стр. 74 из 221

План потолков · 1-й этаж

Уровни и марки потолков, короба с подсветкой, ниши под шторы, люки, вырезы · отметки низа от ±0,000 (чистый пол 1-го этажа) · размеры в мм

ПРЕДВАРИТЕЛЬНО · не для производства работ · открыто пунктов: 15 (реестр — л. 8–10)

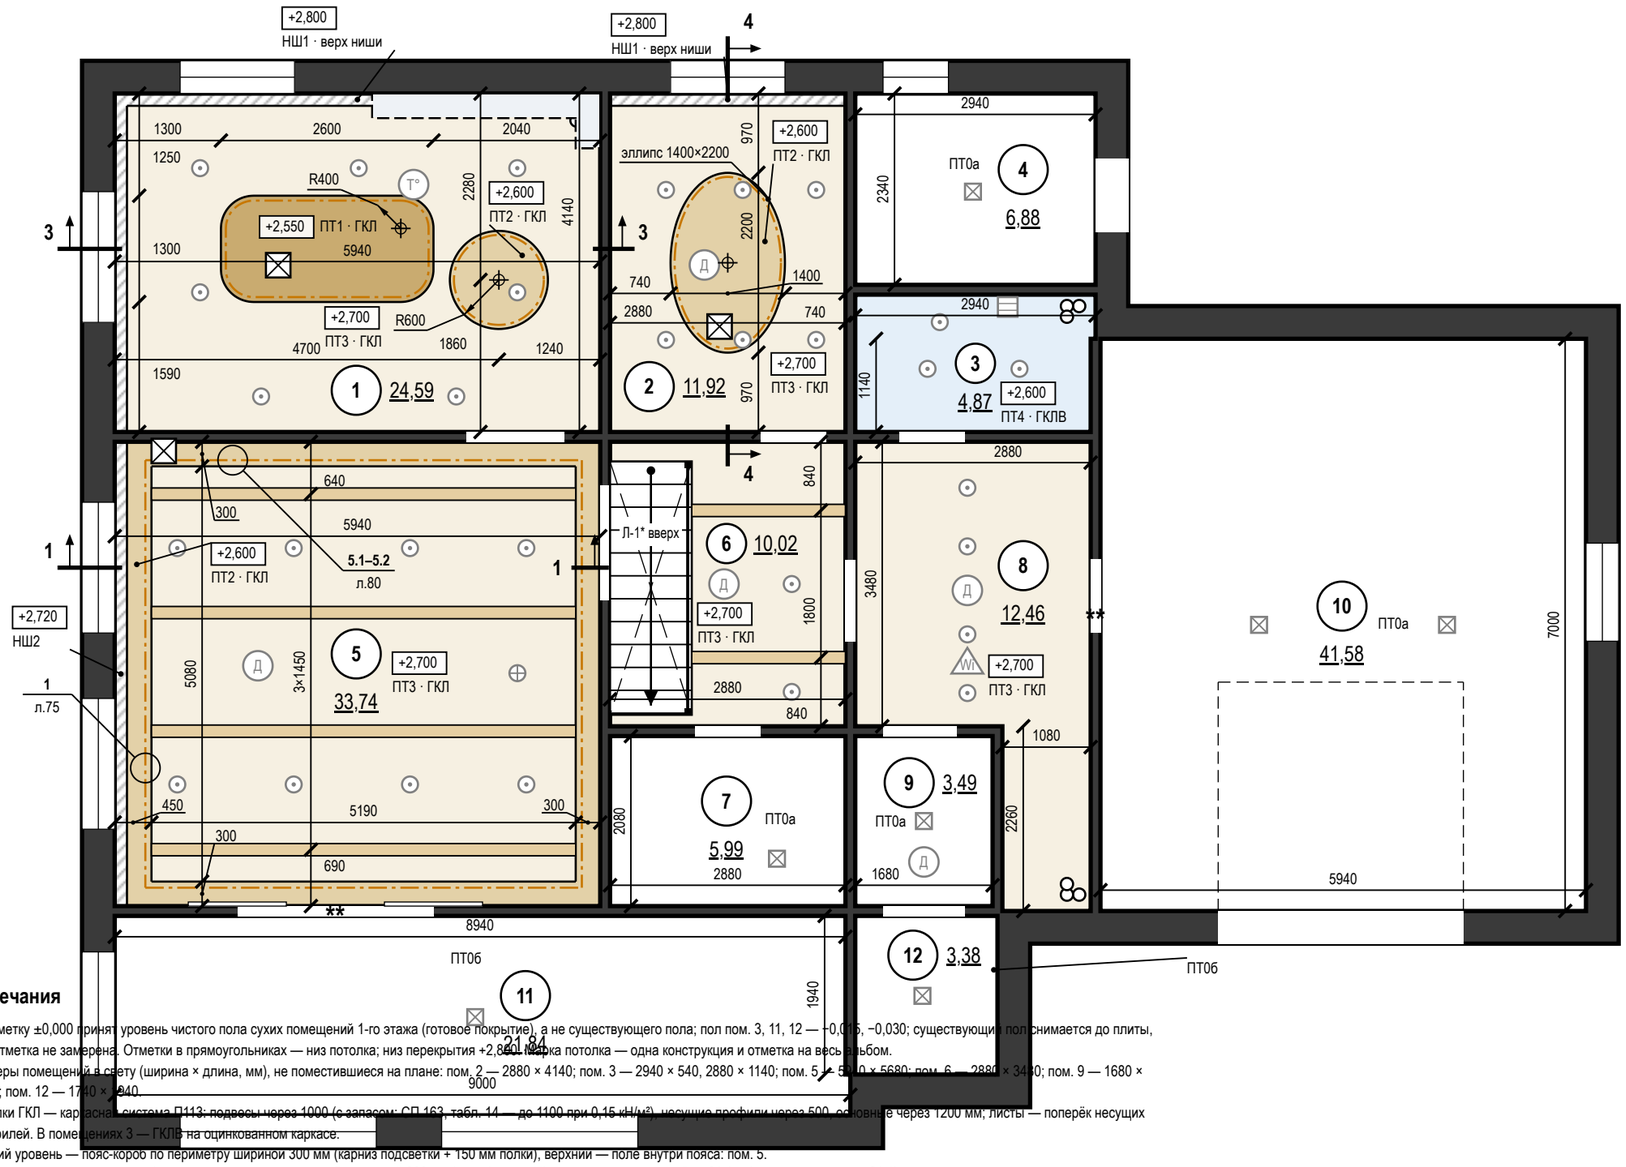

Ведомость потолков

Пом.	Марка	Конструкция	Низ / верх ниши	S, м²	Q
1	ПТ1	ГКЛ П113, остров + LED	+2,550	3,24	Q3
1	ПТ2	ГКЛ П113, круг + LED	+2,600	1,13	Q3
1	ПТ3	ГКЛ П113	+2,700	18,73	Q3
1	НШ1	ниша под шторы 150×100	+2,800	1,49	
2	ПТ2	ГКЛ П113, эллипс + LED	+2,600	2,42	Q3
2	ПТ3	ГКЛ П113	+2,700	9,07	Q3
2	НШ1	ниша под шторы 150×100	+2,800	0,43	
3	ПТ4	ГКЛВ П113	+2,600	4,87	Q3
4, 7, 9, 10	ПТ0а	Потолок под покраску	+2,800	57,94	
5	ПТ2	ГКЛ П113, короб LED	+2,600	6,52	Q3
5	ПТ3	ГКЛ П113	+2,700	26,37	Q3
5	НШ2	ниша под шторы 150×120	+2,720	0,85	
6	ПТ3	ГКЛ П113	+2,700	6,92	Q3
8	ПТ3	То же	+2,700	12,46	Q3
11, 12	ПТ0б	Потолок под покраску (летнее помещение)	+2,800	25,22	
		Итого		**177,66**	

Условные обозначения

- ПТ1 — ГКЛ по каркасу П113, низ +2,550
- ПТ2 — ГКЛ по каркасу П113, низ +2,600
- ПТ3 — ГКЛ по каркасу П113, низ +2,700
- ПТ4 — ГКЛВ по каркасу П113, низ +2,600
- ПТ0а — потолок под покраску, без подвесного потолка, низ +2,800
- ПТ0б — потолок под покраску (летнее помещение), без подвесного потолка, низ +2,800
- НШ1 — ниша под шторы 150×100, верх +2,800
- НШ2 — ниша под шторы 150×120, верх +2,720
- граница уровней потолка (перепад)
- проём лестницы в перекрытии: потолка нет, по кромке — борт ГКЛ до перекрытия
- LED-лента в нише подсветки (карниз короба, ниша фигуры)
- стояк: К1 — канализация, В1 — ХВС, Т3 — ГВС
- балка декоративная 150×120 мм
- люк ревизии в потолке 300×300 мм (доступ к БП LED)

Примечания

1. За отметку ±0,000 принят уровень чистого пола сухих помещений 1-го этажа (готовое покрытие), а не существующего пола; пол пом. 3, 11, 12 — −0,015; −0,030; существующий пол снимается до плиты, его отметка не замерена. Отметки в прямоугольниках — низ потолка; низ перекрытия +2,800. Марка потолка — одна конструкция и отметка на весь альбом.
2. Размеры помещений в свету (ширина × длина, мм), не поместившиеся на плане: пом. 2 — 2880 × 4140; пом. 3 — 2940 × 540, 2880 × 1140; пом. 5 — 5940 × 5680; пом. 6 — 2880 × 3480; пом. 9 — 1680 × 2080; пом. 12 — 1740 × 1940.
3. Потолки ГКЛ — каркасная система П113: подвесы через 1000 (с запасом; СП 163, табл. 14 — до 1100 при 0,15 кН/м²), несущие профили через 500, основные через 1200 мм; листы — поперёк несущих профилей. В помещениях 3 — ГКЛВ на оцинкованном каркасе.
4. Нижний уровень — пояс-короб по периметру шириной 300 мм (карниз подсветки + 150 мм полки), верхний — поле внутри пояса: пом. 5.
5. LED-лента в алюминиевом профиле посередине карниза короба шириной 300 мм (узел 1, лист 75); длина по плану: пом. 5 — 21,1 м (в плане освещения 21,1).
6. Балки декоративные 150×120 мм, фальш-балка, массив лиственницы под маслом: пом. 5 — 4 шт., 20,8 м; пом. 6 — 2 шт., 3,8 м, низ +2,580; крепление — на закладной брус 50×50 к каркасу П113, саморезы скрыто.
7. Ниши под шторы 150×100 мм — на всю длину стены с окном; карниз — на закладной до обшивки (узел 2 — пом. 1, 2, лист 75; узел 3 — пом. 5, лист 76).
8. Примыкание к стенам: теневой шов 15 мм, техзазор 3 мм — пом. 2, 5, по стенам, выровненным штукатуркой (узел 1); пом. 1, 3, 6, 8 — разделительная лента.
9. Светильники и потолочные устройства — подложка с планов освещения, слаботочных систем и вентиляции (положение — по ним); вырезы и закладные — по ведомости на листе, до обшивки; отверстия не совмещать с профилями, глубина корпуса светильника до 70 мм.
10. Разрезы 1–1, 3–3, 4–4 — лист 75; узлы 1, 2 — лист 75; узлы 3, 4 — лист 76; узел 6 — лист 77; сечения М 1:10 по помещениям — листы 79, 80.
11. Узлы по выноскам на плане: узлы 1, 2 — лист 75; узлы 3, 4 — лист 76; узел 6 — лист 77; сечения М 1:10 по помещениям — листы 79, 80.
12. Шпаклевание ГКЛ и условия приёмки — Q3: рассеянный дневной свет, осмотр с 2 м; боковой свет не оценивается.
13. Ведомость вырезов и закладных в потолке (1-й этаж) — на листе 76; вырезы и закладные — до обшивки.
14. Пом. 1: короб воздуховода кухонной вытяжки ГКЛ 300×200 мм (ширина от стены × высота), низ +2,600, длина 2,86 м — по трассе плана вентиляции, вдоль стен до входа в канал под воздуховод Ø125; каркас ПН 28×27 по стене и плите, ПП 60×27, лист ГКЛ 12,5.
15. Люки ревизии 300×300 мм — по центру блоков питания LED (БП3, БП4, БП1; координаты — план освещения).
16. Пом. 6: над маршем лестницы Л-1* — проём перекрытия 1000×3100 мм; потолок ГКЛ по кромке проёма закрыт бортом до перекрытия (ГКЛ по ПН 28×27, длина кромки 5,1 м); светильники и устройства в проёме не ставятся.
17. Основание потолка ПТ0а, ПТ0б — по проекту КР дома: конструкция перекрытия в исходных данных не задана (открытый вопрос К-5).
18. Сечения потолков М 1:10: пом. 1 — 1.1, 1.2, 1.3 (лист 79); пом. 2 — 2.1, 2.2, 2.3 (лист 79).

Условные обозначения (продолжение)

- светильник встраиваемый — подложка с плана освещения
- светильник накладной — подложка с плана освещения
- светильник подвесной — подложка с плана освещения
- Д — извещатель дымовой на потолке — подложка
- Т° — извещатель тепловой на потолке — подложка
- Wi — точка доступа Wi-Fi на потолке — подложка
- решётка вытяжки в потолке — подложка с плана вентиляции
- короб воздуховода вытяжки ГКЛ (трасса — план вентиляции)
- линия разреза; у стен: помещения устройства — направление взгляда
- место узла и сечений М 1:10; номер узла или сечения на полке, под полкой — лист
- +2,600 — отметка низа потолка, м (у ниши под шторы — верх ниши); под ней марка потолка
- 1 — номер помещения, площадь м²
- фрагменты (лист 74), 2 (лист 76)
- ** — высоты мебели и дверных блоков сверены с низом потолка в разрезах; пиктограмма фигур и ленты ниш — там же; размеры фигурных уровней

1000 мм · печать 1:1

Допущения и предложения на листе. Знак «*» принято (замерить). Знак «**» предложено (согласовать). См. лист открытых вопросов (листы 8–10).

Изм.	Кол.уч	Лист	№ док.	Подп.	Дата
Разраб.		Кырлан А.С.			04.11.26
Пров.					
ГИП					
Н. контр.					
Утв.					

ГД-2026-010-АИ

Дом 331 м²

Общая площадь 270,67* м² · * размеры приняты, не замерены (реестр — л. 8–10, К-1)

Дизайн-проект интерьера

Стадия	Лист	Листов
РП	73	216

План потолков · 1-й этаж

М 1:75


Кырлан Александр Сергеевич

выпуск 04.11.2026 · 2a77323a49 · стр. 75 из 221

План потолков · Мансарда

Уровни и марки потолков, короба с подсветкой, ниши под шторы, люки, вырезы · отметки низа от ±0,000 (чистый пол 1-го этажа) · размеры в мм

ПРЕДВАРИТЕЛЬНО · не для производства работ · открыто пунктов: 15 (реестр — л. 8–10)

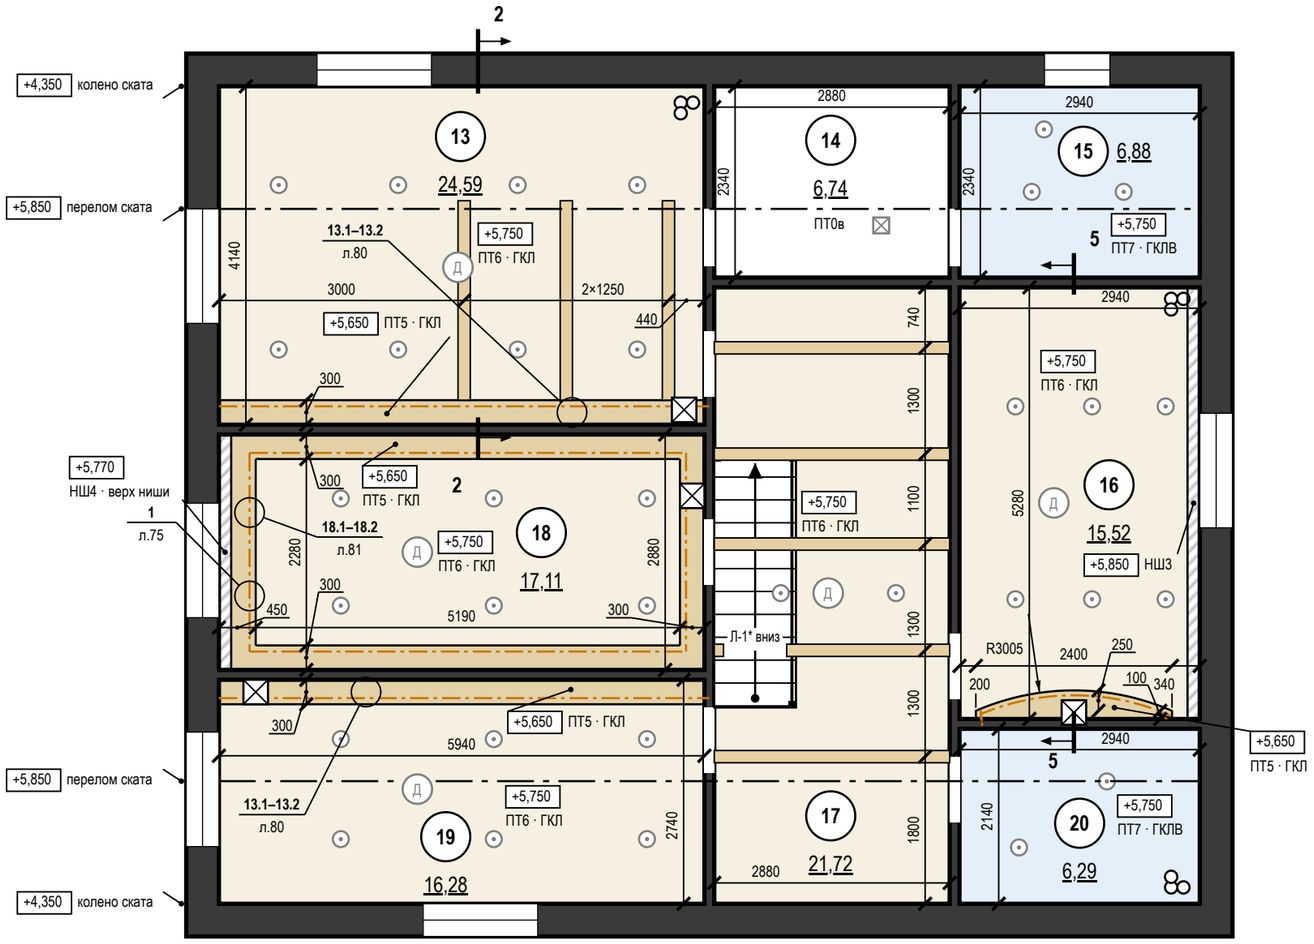

Условные обозначения

- ПТ5 — ГКЛ по каркасу П113, низ +5,650, пояс-короб с карнизом LED
- ПТ6 — ГКЛ по каркасу П113, низ +5,750
- ПТ7 — ГКЛВ по каркасу П113, низ +5,750
- ПТ0в — обшивка скатов и горизонтальной части мансарды (конструкция — по проекту КР), окраска, низ горизонтальной части +5,850
- НШ3 — ниша под шторы 150×100, верх +5,850
- НШ4 — ниша под шторы 150×120, верх +5,770
- граница уровней потолка (перепад)
- LED-лента в нише подсветки (карниз короба, ниша фигуры)
- линия перелома потолка мансарды: скат → горизонтальная часть; отметки ската — у плана
- стояк: К1 — канализация, В1 ХВС, Т3 — ГВС
- балка декоративная 150×120 мм
- люк ревизии в потолке 300×300 мм (доступ к БП LED)
- светильник встраиваемый подложка с плана освещения
- светильник накладной — подложка с плана освещения
- Д — извещатель дымовой на потолке подложка
- линия разреза у стен помещения, стрелка — направление взгляда

Ведомость потолков

Пом.	Марка	Конструкция	Низ / верх ниши	S, м²	Q
13	ПТ5	ГКЛ П113, короб LED	+5,650	1,78	Q3
13	ПТ6	ГКЛ П113	+5,750	22,81	Q3
14	ПТ0в	Обшивка скатов и горизонтальной части мансарды (конструкция — по проекту КР), окраска	+5,850	6,74	
15	ПТ7	ГКЛВ П113	+5,750	6,88	Q3
16	ПТ5	ГКЛ П113, дуга + LED	+5,650	0,64	Q3
16	ПТ6	ГКЛ П113	+5,750	14,09	Q3
16	НШ3	ниша под шторы 150×100	+5,850	0,79	
17	ПТ6	ГКЛ П113	+5,750	21,72	Q3
18	ПТ5	ГКЛ П113, короб LED	+5,650	4,84	Q3
18	ПТ6	ГКЛ П113	+5,750	11,84	Q3
18	НШ4	ниша под шторы 150×120	+5,770	0,43	
19	ПТ5	ГКЛ П113, короб LED	+5,650	1,78	Q3
19	ПТ6	ГКЛ П113	+5,750	14,50	Q3
20	ПТ7	ГКЛВ П113	+5,750	6,29	Q3
		Итого		**115,13**	

Ведомость вырезов и закладных в потолке

Марка	Устройство	Кол.	Пом.
	Светильник встраиваемый (марки — план освещения)	33	13, 15, 16, 17, 18, 19, 20
	Светильник накладной (марки — план освещения)	1	14
ИП7…ИП11	Извещатель дымовой	5	13, 16, 17, 18, 19
	Люк ревизии 300×300	4	13, 16, 18, 19

Условные обозначения (продолжение)

+3,150 — отметка низа потолка (подшторы — верх ниши), под ним марка потолка

+3,086 — расчётный по пирогу пола, не замерен; существующий пол снимается до плиты, его отметка не замерена. Отметки в прямоугольниках — низ потолка. Марка потолка — одна конструкция и отметка на весь альбом.

1 — номер помещения, площадь м²

Примечания

1. За отметку ±0,000 принят уровень чистого пола 1-го этажа (плоское покрытие) относительно существующего пола; чистый пол всех этажей помещений 2 этажа — +3,150, пол ванных 15, 20 — +3,135, верх плиты перекрытия +3,086 — расчётный по пирогу пола, не замерен; существующий пол снимается до плиты, его отметка не замерена. Отметки в прямоугольниках — низ потолка. Марка потолка — одна конструкция и отметка на весь альбом.
2. Размеры помещений в свету (ширина × длина, мм), не поместившиеся на плане: пом. 13 — 5940 × 4140; пом. 17 — 2880 × 7540; пом. 18 — 5940 × 2880.
3. Мансарда: потолок по скатам кровли — от +4,350 у наружных стен вдоль конька до +5,850 у линий перелома (штрихпунктир), между ними — горизонтальная часть +5,850 (в пом. 13, 15, 16, 17, 18, 19, 20 горизонтальная часть подшита ниже — по марке и отметке потолка; скат обшит до линии подшивки); над слуховыми окнами скат поднят до горизонтальной части. Обшивка скатов — по стропилам с пароизоляцией по проекту КР.
4. Потолки ГКЛ — каркасная система П113: подвесы через 1000 (с запасом: СП 163, табл. 14 — до 1100 при 0,15 кН/м²), несущие профили через 500, основные через 1200 мм; листы — поперёк несущих профилей. В помещениях 15, 20 — ГКЛВ на оцинкованном каркасе.
5. Нижний уровень — пояс-короб по периметру шириной 300 мм (карниз подсветки + 150 мм полки), верхний — поле внутри пояса: пом. 18.
6. Короб-полоса у одной стены (не по периметру): ПТ5 шириной 300 мм — пом. 13 у стены В, пом. 19 у стены А.
7. LED-лента в алюминиевом профиле посередине карниза короба шириной 300 мм (узел 1, лист 75); длина по плану: пом. 13 — 6,0 м (в плане освещения 6); пом. 18 — 15,5 м (в плане освещения 15,5); пом. 19 — 6,0 м (в плане освещения 6).
8. Балки декоративные 150×120 мм, фальш-балка, массив лиственницы под маслом: пом. 13 — 3 шт., 7,3 м; пом. 17 — 5 шт., 14,4 м, низ +5,630; крепление — на закладной брус 50×50 к каркасу П113, саморезы скрыто.
9. Ниши под шторы 150×100 мм — на всю длину стены с окном; карниз — на закладной до обшивки (узел 2 — пом. 16, лист 75; узел 3 — пом. 18, лист 76).
10. Примыкание к стенам: теневой шов 15 мм, техзазор 3 мм — пом. 16, 18, по стенам, выровненным штукатуркой (узел 1); пом. 13, 15, 17, 19, 20 — разделительная лента.
11. Светильники и потолочные устройства — подложка с планов освещения, слаботочных систем и вентиляции (положение — по ним); вырезы и закладные — по ведомости на листе, до обшивки; отверстия не совмещать с профилями, глубина корпуса светильника до 70 мм.
12. Разрезы 2–2 — лист 75; 5–5 — лист 77; высоты мебели и дверных блоков сверены с низом потолка в разрезах; гибка бортов фигур и ленты ниш — там же; размеры фигурных уровней — фрагмент 3 (лист 78).
13. Узлы по выноскам на плане: узлы 1, 2 — лист 75; узел 3 — лист 76; узел 5 — лист 77; сечения М 1:10 по помещениям — листы 80, 81.
14. Шпаклевание ГКЛ и условия приёмки — Q3: рассеянный дневной свет, осмотр с 2 м; боковой свет не оценивается.
15. Люки ревизии 300×300 мм — по центру блоков питания LED (БП6, БП7, БП8, БП9; координаты — план освещения).
16. Сечения потолков М 1:10: пом. 16 — 16.1, 16.2, 16.3 (листы 80, 81).

1000 мм · печать 1:1

Допущения и предложения на листе. Основа листа: размеры и контуры этажей подобраны проектировщиком по составу помещений и площадям этажей с картинки 470 px (размеры на ней не читаются); обмер и исходный проект — задание (К-1); высоты: 1-й этаж 2800 мм, мансарда 2700 мм (горизонтальная часть) приняты; скаты кровли мансарды приняты по картинке: колено 1200 мм, уклон 45°, конёк вдоль длинной стороны; проект КР — задание (К-2); наружные стены 400 мм, перегородки 120 мм приняты (К-1); разрешённая мощность 15 кВт принята по типовым ТУ для частного дома (К-4); подрайон климата не задан — принят не северный (жилые от 2,5 м) (К-7). Знак «*» — принято, не замерено и не подтверждено (замерить на объекте): К-2: отметка чистого пола этажа «Мансарда» +3,150 — принята без источника, все отметки мансарды считаются от неё; К-6: Л-1 — габарит марша снят с картинки заказчика (11 проступей в холле 3,6 м), а до отм. +3,150 нужно 18 подъёмов — одномаршевая не встаёт: решение по К-6. См. лист открытых вопросов (лист 8, записи К-1, К-2, К-4, К-6, К-7); по листу — К-2, К-7.

Изм.	Кол.уч	Лист	№ док.	Подп.	Дата
Разраб.		Кырлан А.С.			04.11.26
Пров.					
ГИП					
Н. контр.					
Утв.					

ГД-2026-010-АИ

Дом 331 м²

Общая площадь 270,67* м² · * размеры приняты, не замерены (реестр — л. 8–10, К-1)

Дизайн-проект интерьера

Стадия	Лист	Листов
РП	74	216

План потолков · Мансарда

М 1:75

Кырлан Александр Сергеевич


выпуск 04.11.2026 № 2a77323a49 · стр. 76 из 221

Разрезы и узлы потолков

Разрезы по потолкам с отметками уровней · узлы коробов и ниш · размеры в мм


Разрез 1–1 (М 1:40)

Пом. 5 Гостиная

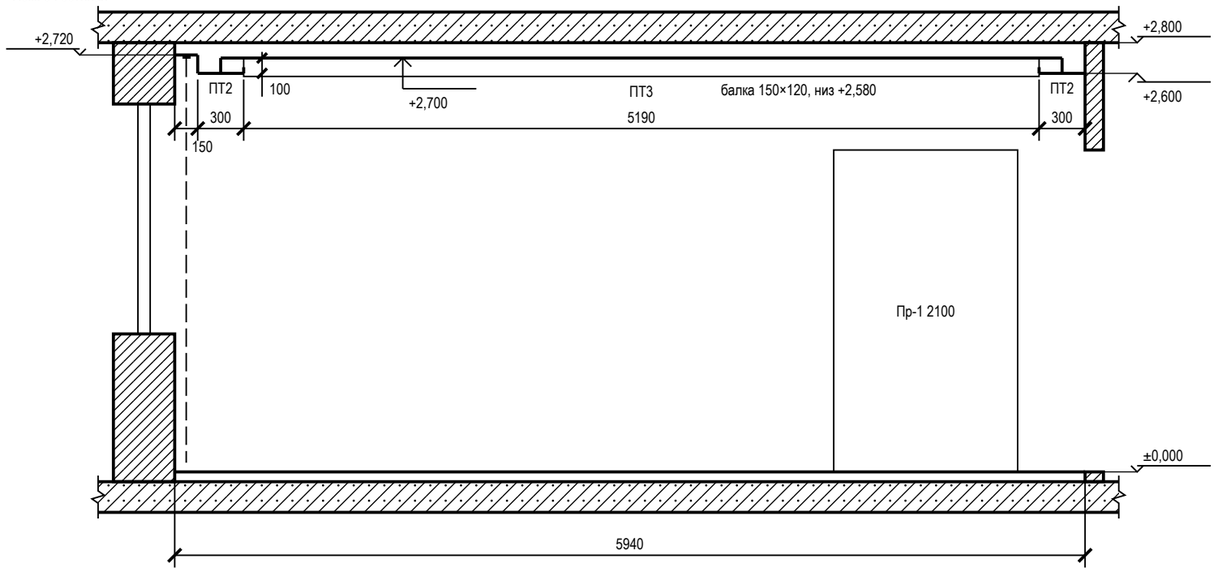


Разрез 2–2 (М 1:40)

Пом. 13 Спальня мастер (мансарда, потолок по скату)

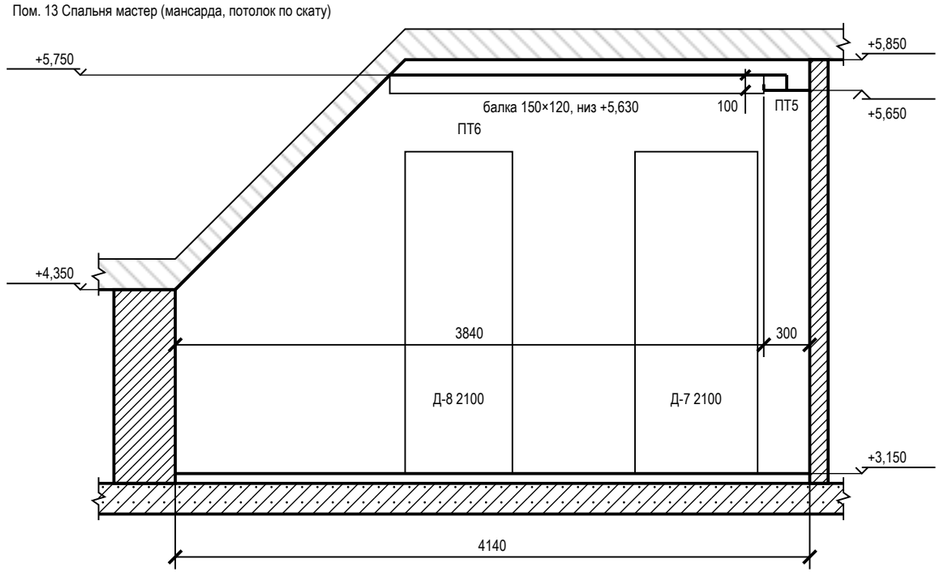

1 Короб с LED-подсветкой, теневой шов (М 1:10)

Пом. 5, 13, 18, 19; карниз 150×100, щель под свет 60 мм

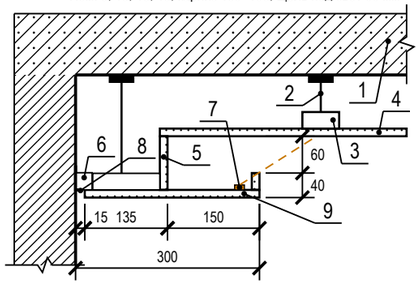


1 — плита перекрытия
2 — подвес прямой, шаг 1000 мм
3 — ПП 60×27: несущие через 500, основные через 1200 мм
4 — ГКЛ 12,5 по П113 — верхний уровень
5 — задняя стенка и бортик карниза — ГКЛ 12,5
6 — ПН 28×27 по периметру, к стене через 500 мм
7 — LED-лента в алюминиевом профиле
8 — теневой профиль: шов 15 мм, зазор 3 мм — пом. 5, 18; пом. 13, 19 — разделительная лента
9 — низ короба — ГКЛ 12,5 по ПП 60×27

Отметки по помещениям, м

Пом.	низ короба	верх. уровень	низ перекрытия
5	+2,600	+2,700	+2,800
13, 18, 19	+5,650	+5,750	+5,850

2 Ниша под шторы (М 1:10)

Пом. 1, 2, 16; без подсветки; закладные под карниз — до обшивки

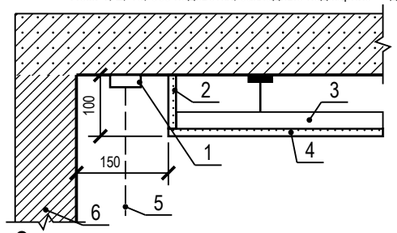

1 — карниз (шина), высота с верхом портьеры 100 мм
2 — стенка ниши — ГКЛ 12,5
3 — ПП 60×27 — каркас короба
4 — низ короба нижнего уровня — ГКЛ 12,5
5 — портьера
6 — стена с окном

Отметки по помещениям, м

Пом.	низ потолка	верх ниши	низ перекрытия
1, 2	+2,700	+2,800	+2,800
16	+5,750	+5,850	+5,850

Условные обозначения

- плита перекрытия в сечении
- стена в сечении
- потолок ГКЛ в сечении; под линией — марка потолка (план потолков)
- мебель и дверные проёмы за секущей плоскостью; число — марка и верх от чистого пола, мм
- портьера в нише под шторы
- балка декоративная: в сечении — заливка, за плоскостью — тонкой линией; низ балки — подписью у балки или отметкой справа
- кровля над мансардой (условно, по проекту КР)

Допущения и предложения на листе

Основа листа: размеры и контуры этажей подобраны проектировщиком по составу помещений и площадям этажей с картинки 470 px (размеры на ней не читаются); обмер и исходный проект — задание (К-1); высоты: 1-й этаж 2800 мм, мансарда 2700 мм (горизонтальная часть) приняты; скаты кровли мансарды приняты по картинке: колено 1200 мм, уклон 45°, конёк вдоль длинной стороны; проект КР — задание (К-2); наружные стены 400 мм, перегородки 120 мм приняты (К-1); разрешённая мощность 15 кВт принята по типовым ТУ для частного дома (К-4); подрайон климата не задан — принят не северный (жилые от 2,5 м) (К-7).
См. лист открытых вопросов (лист 8, записи К-1, К-2, К-4, К-7).

Примечания

1. Разрезы — по линиям 1–1, 2–2 на плане потолков. Отметки — от ±0,000 (чистый пол 1-го этажа), м; размеры — мм.
2. Высоты мебели и дверных блоков за секущей плоскостью сверены с низом потолка над ними: верх ниже низа короба и поля.
3. ГКЛ 12,5 мм по каркасу П113; перепад уровней и бортик карниза — ГКЛ по ПП 60×27 (узел 1 — на этом листе). Ниша под шторы — на всю длину стены с окном, карниз на закладной до обшивки (узел 2 — на этом листе; узел 3 — лист 76).
4. Толщины плит перекрытия и пирога пола показаны условно.
5. Сечения потолков по помещениям М 1:10 (отметки помещения, профили, подвесы, крепёж, изделия) — листы 79–81.
6. Ведомость объёмов потолков (лист ГКЛ, профиль, подвесы, лента, блоки питания, люки) — на листе 78.
7. Фрагменты 1, 3, 2 — помещения с фигурными уровнями (размеры фигур, радиусы, отметки) — на листах 77, 78.

1000 мм · печать 1:1

Изм.	Кол.уч	Лист	№ док.	Подп.	Дата
Разраб.		Кырлан А.С.			04.11.26
Пров.					
ГИП					
Н. контр.					
Утв.					

ГД-2026-010-АИ

Дом 331 м²

Общая площадь 270,67* м² · * размеры приняты, не замерены (реестр — л. 8–10, К-1)

Дизайн-проект интерьера

Стадия	Лист	Листов
РП	75	216

Разрезы и узлы потолков

М 1:40; 1:10

Кырлан Александр Сергеевич


выпуск 04.11.2026 № 2a77323a49 · стр. 77 из 221

Разрезы и узлы потолков (продолжение)

Разрезы по потолкам с отметками уровней · узлы коробов и ниш · ведомость вырезов и закладных · размеры в мм


Разрез 3–3 (М 1:40)

Пом. 1 Кухня-столовая

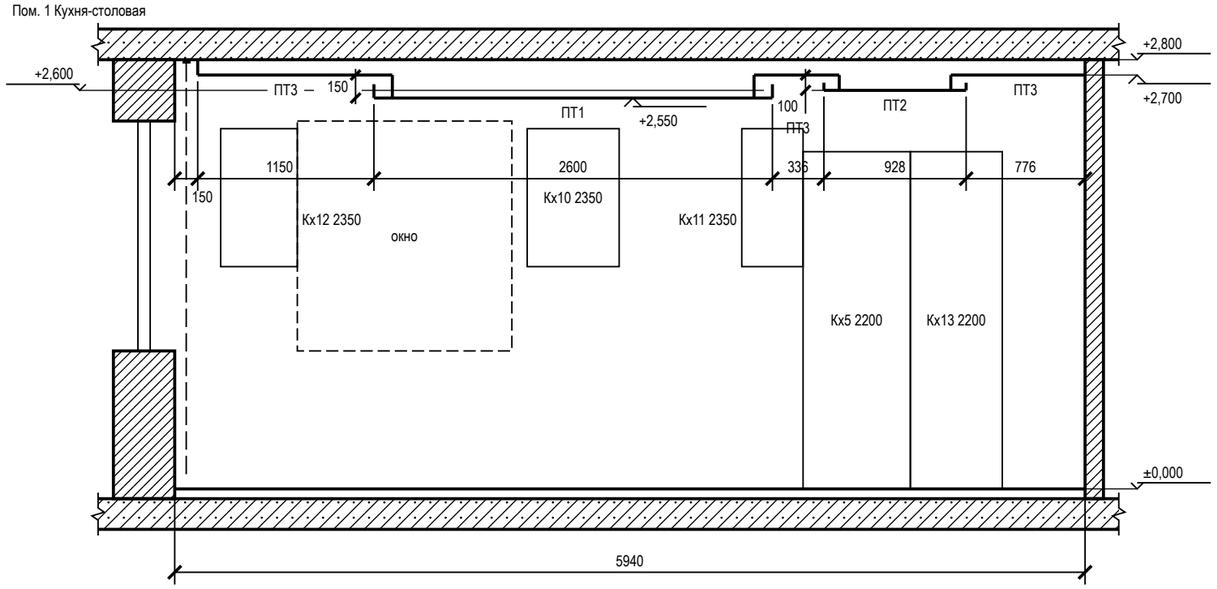


Разрез 4–4 (М 1:40)

Пом. 2 Кабинет-гостевая

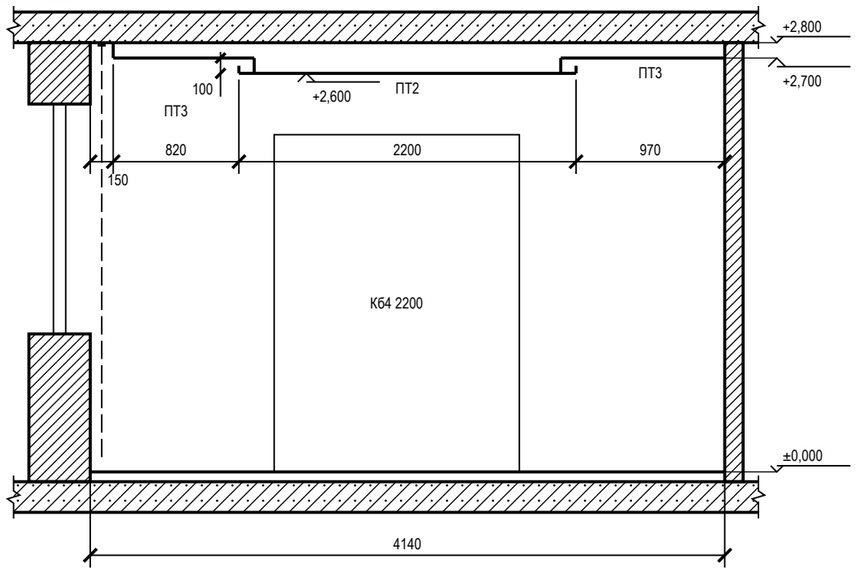

3 Ниша под шторы (М 1:10)


Пом. 5, 18; без подсветки; закладные под карниз — до обшивки

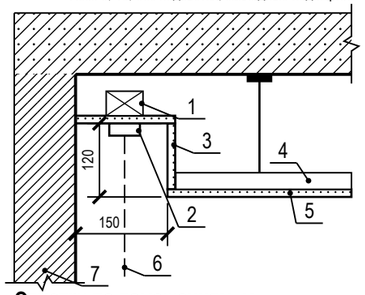

1 — закладная под карниз — брус 40×50
2 — карниз (шина), высота с верхом портьеры 100 мм
3 — стенка и потолок ниши — ГКЛ 12,5
4 — ПП 60×27 — каркас короба
5 — низ короба нижнего уровня — ГКЛ 12,5
6 — портьера
7 — стена с окном

4 Ниша LED фигурного уровня (М 1:10)

Пом. 1; карниз 120×100, щель под свет 60 мм

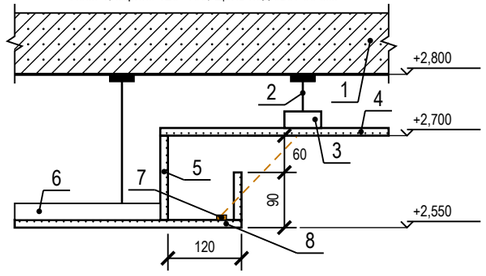

1 — плита перекрытия
2 — подвес прямой, шаг 1000 мм
3 — ПП 60×27: несущие через 500, основные через 1200 мм
4 — ГКЛ 12,5 по П113 — верхний уровень
5 — задняя стенка и бортик карниза — ГКЛ 12,5
6 — ПП 60×27 каркаса нижнего уровня, ПН по контуру фигуры (на дуге — с надрезами)
7 — LED-лента в алюминиевом профиле
8 — низ короба — ГКЛ 12,5 по ПП 60×27

Отметки по помещениям, м

Пом.	низ потолка	верх ниши	низ перекрытия
5	+2,600	+2,720	+2,800
18	+5,650	+5,770	+5,850

Ведомость вырезов и закладных в потолке · 1-й этаж

Марка	Устройство	Кол.	Пом.
	Светильник встраиваемый (марки — план освещения)	30	1, 2, 3, 5, 6, 8
	Светильник накладной (марки — план освещения)	7	4, 7, 9, 10, 11, 12
	Светильник подвесной (марки — план освещения)	1	5
ИП2, ИП1, ИП6**, ИП3**, ИП12**	Извещатель дымовой	5	2, 5, 6, 8, 9
ИП4	Извещатель тепловой	1	1
АР1**	Точка доступа Wi-Fi, PoE	1	8
ВР2	Решётка вытяжная (вентилятор)	1	3
	Люк ревизии 300×300	3	1, 2, 5

Допущения и предложения на листе

Основа листа: размеры и контуры этажей подобраны проектировщиком по составу помещений и площадям этажей с картинки 470 px (размеры на ней не читаются); обмер и исходный проект — задание (К-1); высоты: 1-й этаж 2800 мм, мансарда 2700 мм (горизонтальная часть) приняты; скаты кровли мансарды приняты по картинке: колено 1200 мм, уклон 45°, конёк вдоль длинной стороны; проект КР — задание (К-2); наружные стены 400 мм, перегородки 120 мм приняты (К-1); разрешённая мощность 15 кВт принята по типовым ТУ для частного дома (К-4); подрайон климата не задан — принят не северный (жилые от 2,5 м) (К-7).

Знак «**» — предложение проектировщика, заказчиком не утверждено (согласовать с заказчиком): ИП6, ИП3 — дымовой автономный вместо теплового образца: жилой дом — автономные дымовые в путях эвакуации (СП 486, пункт сверить по действующей редакции); ИП12 — жилой дом — автономные дымовые извещатели в жилых комнатах и путях эвакуации (СП 486, пункт сверить по действующей редакции); место — центр помещения, не ближе 500 мм к светильнику; АР1 — точка доступа Wi-Fi: число и места.

См. лист открытых вопросов (лист 8, записи К-1, К-2, К-4, К-7).

Примечания

1. Разрезы — по линиям 3–3, 4–4 на плане потолков. Отметки — от ±0,000 (чистый пол 1-го этажа), м; размеры — мм.
2. Высоты мебели и дверных блоков за секущей плоскостью сверены с низом потолка над ними: верх ниже низа короба и поля.
3. ГКЛ 12,5 мм по каркасу П113; узлы коробов и ниш под шторы: узел 1 — лист 75; узел 2 — лист 75; узел 3 — на этом листе; условные обозначения разрезов — на листе 75.
4. Толщины плит перекрытия и пирога пола показаны условно.
5. Ведомость вырезов и закладных в потолке (1-й этаж) — к плану потолков: вырезы и закладные — до обшивки, марки светильников — по плану освещения.

1000 мм · печать 1:1

Изм.	Кол.уч	Лист	№ док.	Подп.	Дата
Разраб.		Кырлан А.С.			04.11.26
Пров.					
ГИП					
Н. контр.					
Утв.					

ГД-2026-010-АИ

Дом 331 м²

Общая площадь 270,67* м² · * размеры приняты, не замерены (реестр — л. 8–10, К-1)

Дизайн-проект интерьера

Стадия	Лист	Листов
РП	76	216

Разрезы и узлы потолков (продолжение)

М 1:40; 1:10

Кырлан Александр Сергеевич


выпуск 04.11.2026 № 2a77323a49 · стр. 78 из 221

Разрезы и узлы потолков (продолжение)

Разрезы по потолкам с отметками уровней · узлы коробов и ниш · фрагменты фигурных уровней · ведомость вырезов и закладных · размеры в мм


Разрез 5–5 (М 1:40)

Пом. 16 Спальня 2 (мансарда, разрез по горизонтальной части)

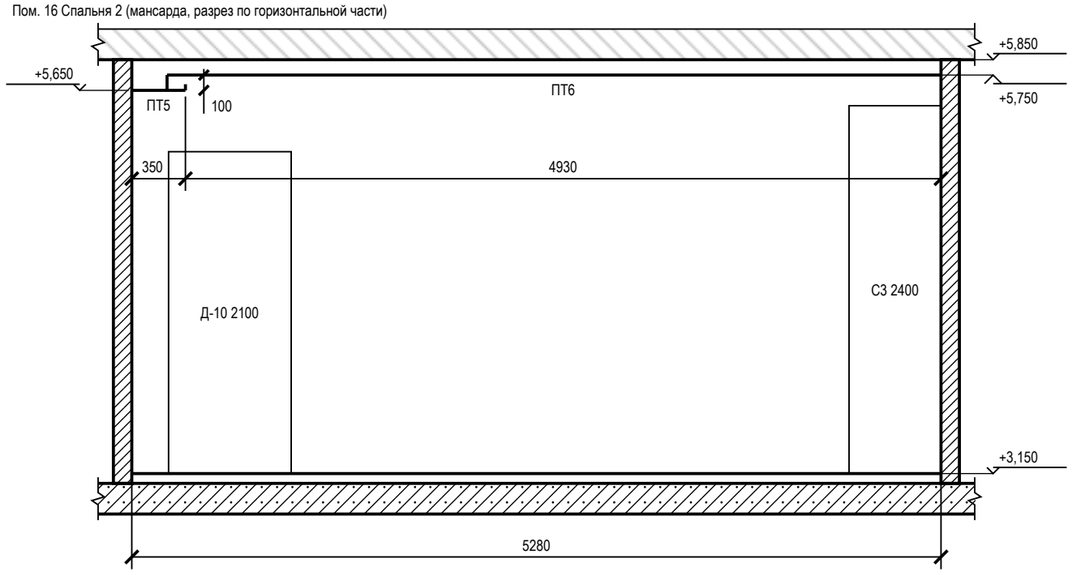

Фрагмент 1. Пом. 1 Кухня-столовая — уровни потолка (М 1:50)

Цепочки — от чистых граней стен; отметки — низ уровня от ±0,000

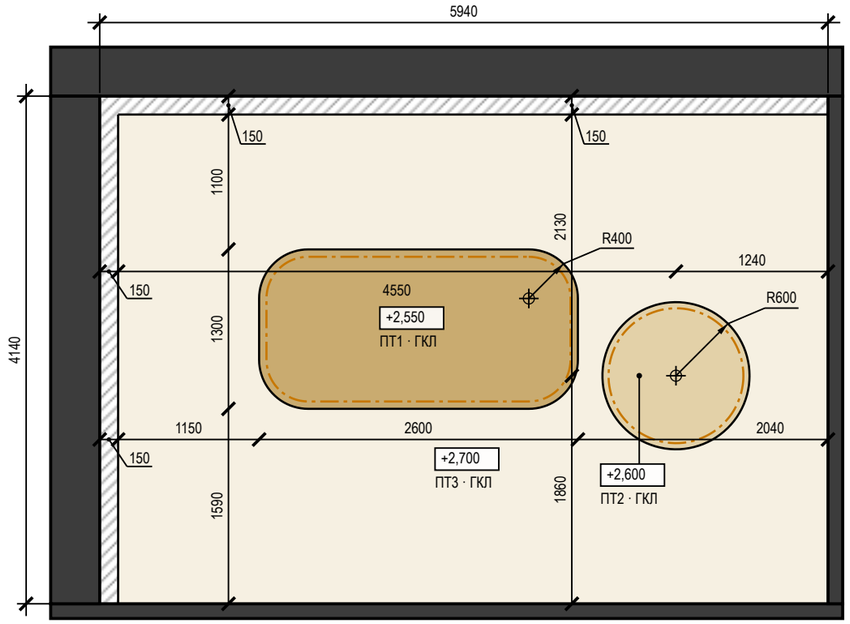


ПТ1 — низ +2,550 · ПТ2 — низ +2,600 · ПТ3 — низ +2,700

LED-лента в нише подсветки (карниз короба, ниша фигуры) · ниша под шторы

5 Ниша LED фигурного уровня (М 1:10)


Пом. 16; карниз 120×100, щель под свет 60 мм

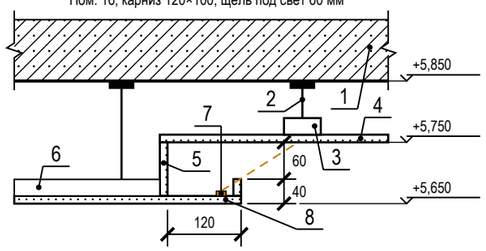

1 — плита перекрытия
2 — подвес прямой, шаг 1000 мм
3 — ПП 60×27: несущие через 500, основные через 1200 мм
4 — ГКЛ 12,5 по П113 — верхний уровень
5 — задняя стенка и бортик карниза — ГКЛ 12,5
6 — ПП 60×27 каркаса нижнего уровня, ПН по контуру фигуры (на дуге — с надрезами)
7 — LED-лента в алюминиевом профиле
8 — низ короба — ГКЛ 12,5 по ПП 60×27

6 Ниша LED фигурного уровня (М 1:10)

Пом. 2; карниз 100×100, щель под свет 50 мм

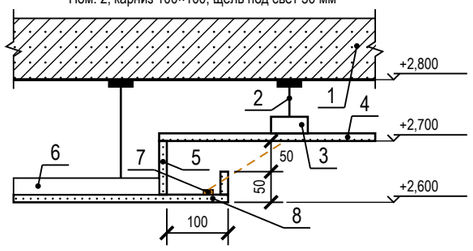

1 — плита перекрытия
2 — подвес прямой, шаг 1000 мм
3 — ПП 60×27: несущие через 500, основные через 1200 мм
4 — ГКЛ 12,5 по П113 — верхний уровень
5 — задняя стенка и бортик карниза — ГКЛ 12,5
6 — ПП 60×27 каркаса нижнего уровня, ПН по контуру фигуры (на дуге — с надрезами)
7 — LED-лента в алюминиевом профиле
8 — низ короба — ГКЛ 12,5 по ПП 60×27

Ведомость вырезов и закладных в потолке · Мансарда

Марка	Устройство	Кол.	Пом.
	Светильник встраиваемый (марки — план освещения)	33	13, 15, 16, 17, 18, 19, 20
	Светильник накладной (марки — план освещения)	1	14
ИП7…ИП11	Извещатель дымовой	5	13, 16, 17, 18, 19
	Люк ревизии 300×300	4	13, 16, 18, 19

Допущения и предложения на листе

Основа листа: размеры и контуры этажей подобраны проектировщиком по составу помещений и площадям этажей с картинки 470 px (размеры на ней не читаются); обмер и исходный проект — задание (К-1); высоты: 1-й этаж 2800 мм, мансарда 2700 мм (горизонтальная часть) приняты; скаты кровли мансарды приняты по картинке: колено 1200 мм, уклон 45°, конёк вдоль длинной стороны; проект КР — задание (К-2); наружные стены 400 мм, перегородки 120 мм приняты (К-1); разрешённая мощность 15 кВт принята по типовым ТУ для частного дома (К-4); подрайон климата не задан — принят не северный (жилые от 2,5 м) (К-7).
См. лист открытых вопросов (лист 8, записи К-1, К-2, К-4, К-7).

Примечания

1. Разрезы — по линиям 5–5 на плане потолков. Отметки — от ±0,000 (чистый пол 1-го этажа), м; размеры — мм.
2. Высоты мебели и дверных блоков за секущей плоскостью сверены с низом потолка над ними: верх ниже низа короба и поля.
3. ГКЛ 12,5 мм по каркасу П113; узлы коробов и ниш под шторы: узел 1 — лист 75; узел 2 — лист 75; узел 3 — лист 76; условные обозначения разрезов — на листе 75.
4. Толщины плит перекрытия и пирога пола показаны условно.
5. Фрагмент 1 — фигурные уровни потолка крупно: привязки краёв и центров фигур к чистым граням стен, радиусы (R) с центрами, хорда и стрелка дуги, отметки низа каждого уровня; цвета уровней — как на плане потолков.
6. Ведомость вырезов и закладных в потолке (Мансарда) — к плану потолков: вырезы и закладные — до обшивки, марки светильников — по плану освещения.
7. Фигурные уровни: борт — ГКЛ по ПН с надрезами (на дуге шаг стоек борта 300 мм при R до 2500, 400 — до 5000) или по гнутому заводскому профилю (СП 163, 6.3.3); гибка: остров пом. 1 R400 — ГКЛ 6,5 мокрой гибкой; круг пом. 1 R600 — ГКЛ 6,5 мокрой гибкой; эллипс пом. 2 R445 — ГКЛ 6,5 мокрой гибкой; дуга пом. 16 R3005 — ГКЛ 12,5 сухой гибкой (СП 163, табл. 9). Лента в нише фигуры по оси: остров пом. 1 — 6,7 м, круг пом. 1 — 3,5 м, эллипс пом. 2 — 5,4 м, дуга пом. 16 — 3,2 м; узел ниши LED фигуры: узел 4 — лист 76 — пом. 1; узел 6 — на этом листе — пом. 2; узел 5 — на этом листе пом. 16.

1000 мм · печать 1:1

Изм.	Кол.уч	Лист	№ док.	Подп.	Дата
Разраб.		Кырлан А.С.			04.11.26
Пров.					
ГИП					
Н. контр.					
Утв.					

ГД-2026-010-АИ

Дом 331 м²

Общая площадь 270,67* м² · * размеры приняты, не замерены (реестр — л. 8–10, К-1)

Дизайн-проект интерьера

Стадия	Лист	Листов
РП	77	216

Разрезы и узлы потолков (продолжение)

М 1:40; 1:50; 1:10

Кырлан Александр Сергеевич

выпуск 04.11.2026 № 2a77323a49 · стр. 79 из 221

Разрезы и узлы потолков (продолжение)


Фрагменты фигурных уровней · ведомость объёмов · размеры в мм

Ведомость объёмов потолков

Позиция	Ед.	Кол.	Пом.
Лист ГКЛ 12,5	м²	205,77	1, 2, 5, 6, 8, 13, 16, 17, 18, 19
Лист ГКЛВ 12,5	м²	18,04	3, 15, 20
Лист ГКЛ арочный 6,5	м²	4,06	1, 2
Борта и карнизы (входят в площади листов выше)	м²	22,93	1, 2, 5, 6, 13, 16, 18, 19
Профиль ПП 60×27	м	601,81	1, 2, 3, 5, 6, 8, 13, 15, 16, 17, 18, 19, 20
Профиль ПН 28×27	м	474,23	1, 2, 3, 5, 6, 8, 13, 15, 16, 17, 18, 19, 20
Подвес прямой	шт.	226	1, 2, 3, 5, 6, 8, 13, 15, 16, 17, 18, 19, 20
Анкер-клин к плите	шт.	226	1, 2, 3, 5, 6, 8, 13, 15, 16, 17, 18, 19, 20
Шуруп TN 3,5×25	шт.	5194	1, 2, 3, 5, 6, 8, 13, 15, 16, 17, 18, 19, 20
Лента армирующая для швов	м	271,01	1, 2, 3, 5, 6, 8, 13, 15, 16, 17, 18, 19, 20
Шпаклёвка для швов	кг	90,34	1, 2, 3, 5, 6, 8, 13, 15, 16, 17, 18, 19, 20
Грунтовка (швы)	л	22,58	1, 2, 3, 5, 6, 8, 13, 15, 16, 17, 18, 19, 20
Лента разделительная по периметру	м	209,80	1, 2, 3, 5, 6, 8, 13, 15, 16, 17, 18, 19, 20
Сплошная шпаклёвка и окраска (площадь развёртки)	м²	225,84	1, 2, 3, 5, 6, 8, 13, 15, 16, 17, 18, 19, 20
Лента LED	м	67,45	1, 2, 5, 13, 16, 18, 19
Требуемая мощность блоков питания	Вт	842	1, 2, 5, 13, 16, 18, 19
Установленная мощность блоков питания	Вт	1450	1, 2, 5, 13, 16, 18, 19
Блок питания LED	шт.	7	1, 2, 5, 13, 16, 18, 19
Люк ревизии	шт.	7	1, 2, 5, 13, 16, 18, 19

Фрагмент 3. Пом. 16 Спальня 2 — уровни потолка (М 1:50)

Цепочки — от чистых граней стен; отметки — низ уровня от ±0,000

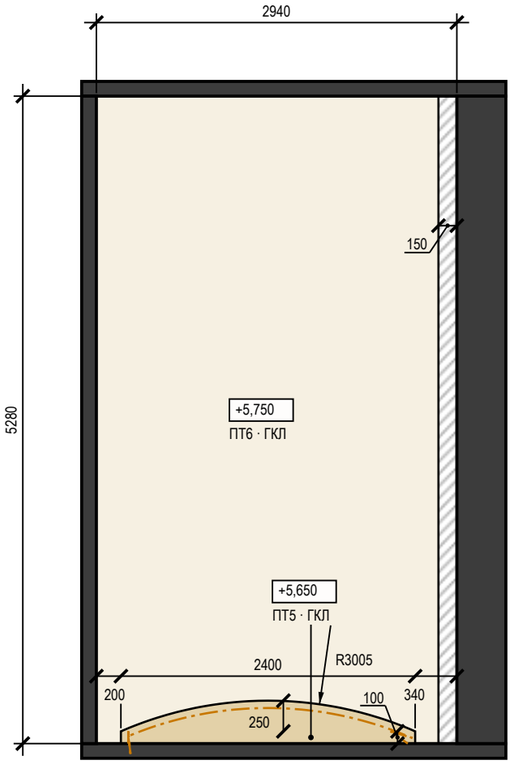


ПТ5 — низ +5,650 ПТ6 — низ +5,750

LED-лента в нише подсветки (карниз короба, ниша фигуры)

ниша под шторы

Фрагмент 2. Пом. 2 Кабинет-гостевая — уровни потолка (М 1:50)

Цепочки — от чистых граней стен; отметки — низ уровня от ±0,000

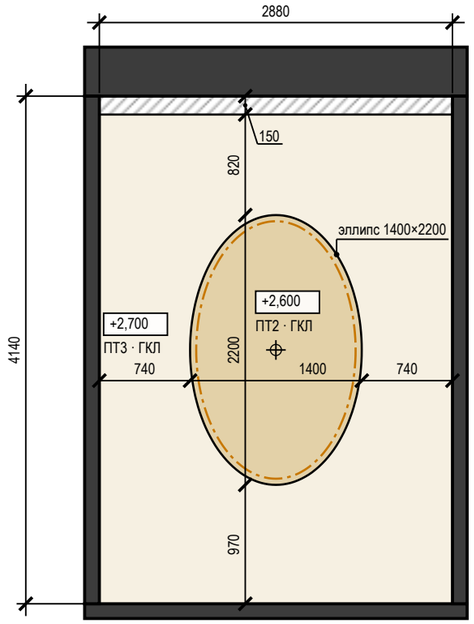

ПТ2 — низ +2,600 ПТ3 — низ +2,700

LED-лента в нише подсветки (карниз короба, ниша фигуры)

ниша под шторы

Допущения и предложения на листе

Основа листа: размеры и контуры этажей подобраны проектировщиком по составу помещений и площадям этажей с картинки 470 px (размеры на ней не читаются); обмер и исходный проект — задание (К-1); высоты: 1-й этаж 2800 мм, мансарда 2700 мм (горизонтальная часть) приняты; скаты кровли мансарды приняты по картинке: колено 1200 мм, уклон 45°, конёк вдоль длинной стороны; проект КР — задание (К-2); наружные стены 400 мм, перегородки 120 мм приняты (К-1); разрешённая мощность 15 кВт принята по типовым ТУ для частного дома (К-4); подрайон климата не задан — принят не северный (жилые от 2,5 м) (К-7).

См. лист открытых вопросов (лист 8, записи К-1, К-2, К-4, К-7).

Примечания

1. ГКЛ 12,5 мм по каркасу П113; узлы коробов и ниш под шторы: узел 1 — лист 75; узел 2 — лист 75; узел 3 — лист 76; условные обозначения разрезов — на листе 75.
2. Фрагменты 3, 2 — фигурные уровни потолка крупно: привязки краёв и центров фигур к чистым граням стен, радиусы (R) с центрами, хорда и стрелка дуги, отметки низа каждого уровня; цвета уровней как на плане потолков.
3. Ведомость объёмов — по геометрии плана потолков: Лист ГКЛ 12,5 — плоскости уровней + борта (без арочных участков); Лист ГКЛВ 12,5 — плоскости уровней + борта; Лист ГКЛ арочный 6,5 — кривая борта × высота борта и стенки ниши × 2 слоя (R400 мокрая гибка, R600 мокрая гибка, R445 мокрая гибка); Борта и карнизы — длина перепада × перепад; Профиль ПП 60×27 — S × (1/шаг несущ. + 1/шаг осн.) + стойки бортов; Профиль ПН 28×27 — периметр стен + 2 × перепады + карнизы; Подвес прямой — по раскладке: S уровня / (шаг осн. × шаг подвесов), пояс уже шага — ряд вдоль пояса, фигура — по контуру; шаг подвесов — не больше табл. 14 СП 163; Анкер-клин к плите — по одному на подвес (Knauf П113); Шуруп TN 3,5×25 — 23 шт./м² (Knauf П113, табл. 2 альбома П 11); Лента армирующая для швов — 1,2 м/м² листа (Knauf); Шпаклёвка для швов — 0,4 кг/м² листа, только швы (Knauf); Грунтовка (швы) — 0,1 л/м² листа, только швы (Knauf); Лента разделительная по периметру — периметр стен под потолком ГКЛ; Сплошная шпаклёвка и окраска (площадь развёртки) — плоскости + борта; расход — по паспорту материала (норма расхода на сплошной слой не подтверждена); Лента LED — по оси карниза и ниши фигуры (план потолков); Требуемая мощность блоков питания — Вт/м × длина × 1,3; Установленная мощность блоков питания — сумма мощностей блоков по плану освещения; Блок питания LED — блоки потолочных лент по плану освещения (БП3, БП4, БП1, БП6, БП7, БП8, БП9); Люк ревизии — план потолков; без запаса на подрезку (при закупке листа: ×1,075 при S > 20 м², ×1,175 — 10–20 м², ×1,275 — < 10 м²).

1000 мм · печать 1:1

Изм.	Кол.уч	Лист	№ док.	Подп.	Дата
Разраб.		Кырлан А.С.			04.11.26
Пров.					
ГИП					
Н. контр.					
Утв.					

ГД-2026-010-АИ

Дом 331 м²

Общая площадь 270,67* м² · * размеры приняты, не замерены (реестр — л. 8–10, К-1)

Дизайн-проект интерьера

Стадия	Лист	Листов
РП	78	216

Разрезы и узлы потолков (продолжение)

М 1:50

Кырлан Александр Сергеевич


выпуск 04.11.2026 № 2a7323a49 · стр. 80 из 221

Сечения потолков М 1:10

Пом. 1, 2 · профили, подвесы, крепёж, изделия · размеры в мм

Сечение 1.1. Ниша LED фигурного уровня (М 1:10)


Пом. 1 Кухня-столовая; карниз 120×100, щель под свет 60 мм

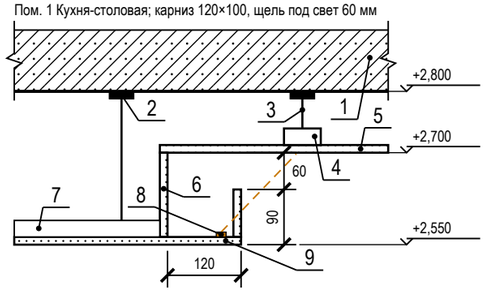

1 — плита перекрытия
2 — анкер-клин к плите — по одному на подвес
3 — подвес прямой, шаг 1000 мм
4 — ПП 60×27: несущие через 500, основные через 1200 мм; соединители одноуровневые, шурупы LN 3,5×9
5 — ГКЛ 12,5 по П113 — верхний уровень; шурупы TN 3,5×25 через 170 мм
6 — задняя стенка и бортик карниза — ГКЛ 12,5
7 — ПП 60×27 каркаса нижнего уровня, ПН по контуру фигуры (на дуге — с надрезами)
8 — LED-лента 9,6 Вт/м, 24 В в алюминиевом профиле
9 — низ короба — ГКЛ 12,5 по ПП 60×27

Сечение 1.2. Ниша под шторы (М 1:10)


Пом. 1 Кухня-столовая; без подсветки; закладные под карниз — до обшивки

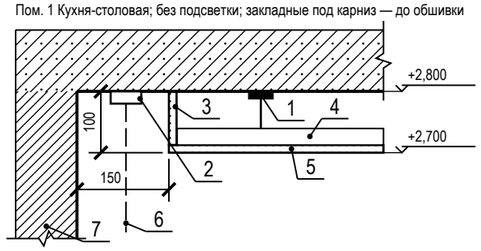

1 — анкер-клин к плите — по одному на подвес; подвес прямой, шаг 1000 мм
2 — карниз (шина), высота с верхом портьеры 100 мм
3 — стенка ниши — ГКЛ 12,5
4 — ПП 60×27 — каркас короба, основные через 1200 мм; соединители одноуровневые, шурупы LN 3,5×9
5 — низ короба нижнего уровня — ГКЛ 12,5; шурупы TN 3,5×25 через 170 мм
6 — портьера
7 — стена с окном

Сечение 1.3. Примыкание потолка к стене (М 1:10)


Пом. 1 Кухня-столовая; примыкание — разделительная лента

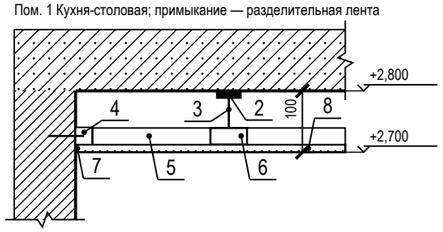

1 — плита перекрытия
2 — анкер-клин к плите — по одному на подвес
3 — подвес прямой, шаг 1000 мм
4 — ПН 28×27 по периметру — дюбель-гвоздь через ≤ 500 мм, не менее 3 на профиль
5 — ПП 60×27 несущий (вид) через 500 мм, в ПН
6 — ПП 60×27 основной (сечение) через 1200 мм; соединители одноуровневые, шурупы LN 3,5×9
7 — лента разделительная по стене, шов зашпаклёван
8 — ГКЛ 12,5 по П113; шурупы TN 3,5×25 через 170 мм

Сечение 2.1. Ниша LED фигурного уровня (М 1:10)


Пом. 2 Кабинет-гостевая; карниз 100×100, щель под свет 50 мм

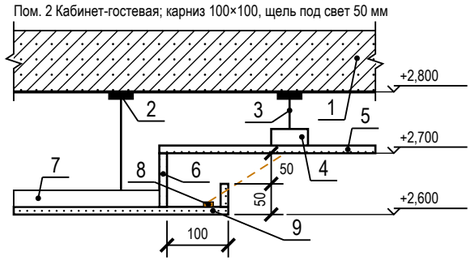

1 — плита перекрытия
2 — анкер-клин к плите — по одному на подвес
3 — подвес прямой, шаг 1000 мм
4 — ПП 60×27: несущие через 500, основные через 1200 мм; соединители одноуровневые, шурупы LN 3,5×9
5 — ГКЛ 12,5 по П113 — верхний уровень; шурупы TN 3,5×25 через 170 мм
6 — задняя стенка и бортик карниза — ГКЛ 12,5
7 — ПП 60×27 каркаса нижнего уровня, ПН по контуру фигуры (на дуге — с надрезами)
8 — LED-лента 9,6 Вт/м, 24 В в алюминиевом профиле
9 — низ короба — ГКЛ 12,5 по ПП 60×27

Сечение 2.2. Ниша под шторы (М 1:10)


Пом. 2 Кабинет-гостевая; без подсветки; закладные под карниз — до обшивки

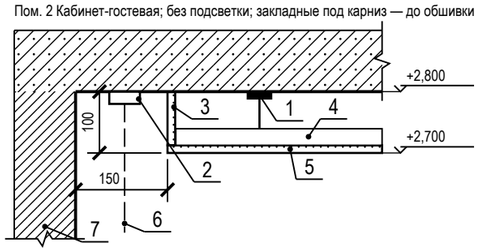

1 — анкер-клин к плите — по одному на подвес; подвес прямой, шаг 1000 мм
2 — карниз (шина), высота с верхом портьеры 100 мм
3 — стенка ниши — ГКЛ 12,5
4 — ПП 60×27 — каркас короба, основные через 1200 мм; соединители одноуровневые, шурупы LN 3,5×9
5 — низ короба нижнего уровня — ГКЛ 12,5; шурупы TN 3,5×25 через 170 мм
6 — портьера
7 — стена с окном

Сечение 2.3. Примыкание потолка к стене (М 1:10)

Пом. 2 Кабинет-гостевая; примыкание — теневой шов

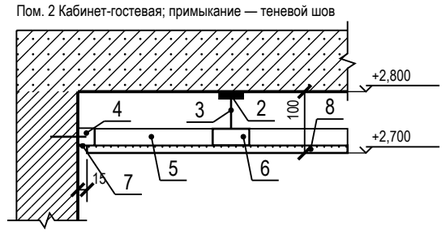

1 — плита перекрытия
2 — анкер-клин к плите — по одному на подвес
3 — подвес прямой, шаг 1000 мм
4 — ПН 28×27 по периметру — дюбель-гвоздь через ≤ 500 мм, не менее 3 на профиль
5 — ПП 60×27 несущий (вид) через 500 мм, в ПН
6 — ПП 60×27 основной (сечение) через 1200 мм; соединители одноуровневые, шурупы LN 3,5×9
7 — теневой профиль: шов 15 мм, зазор 3 мм; стена под шов выровнена
8 — ГКЛ 12,5 по П113; шурупы TN 3,5×25 через 170 мм

Условные обозначения

— · — LED-лента в нише подсветки (карниз короба, ниша фигуры)

Допущения и предложения на листе

Основа листа: размеры и контуры этажей подобраны проектировщиком по составу помещений и площадям этажей с картинки 470 px (размеры на ней не читаются); обмер и исходный проект — задание (К-1); высоты: 1-й этаж 2800 мм, мансарда 2700 мм (горизонтальная часть) приняты; скаты кровли мансарды приняты по картинке: колено 1200 мм, уклон 45°, конёк вдоль длинной стороны; проект КР — задание (К-2); наружные стены 400 мм, перегородки 120 мм приняты (К-1); разрешённая мощность 15 кВт принята по типовым ТУ для частного дома (К-4); подрайон климата не задан — принят не северный (жилые от 2,5 м) (К-7).
См. лист открытых вопросов (лист 8, записи К-1, К-2, К-4, К-7).

Примечания

1. Сечения потолков М 1:10 по помещениям с нишами LED и нишами под шторы: отметки и размеры этого помещения от ±0,000 — чистого пола 1-го этажа (м, мм). Положение — по плану потолков (листы 73, 74): короб и ниша LED — по линиям ленты, ниша под шторы — у стены с окном; типовые узлы по группам помещений — на листе 75.
2. Крепёж: подвес прямой к плите на анкер-клине — по одному на подвес (Knauf П113); ПН к стенам — дюбель-гвоздь через ≤ 500 мм, не менее 3 на профиль (серия 1.045.9-2.08); лист 12,5 — шурупы TN 3,5×25 через 170 мм (СП 163, табл. 15); профили между собой — соединители одноуровневые, шурупы LN 3,5×9.
3. Изделие карниза, профиля LED и галтели подписано артикулом из данных; где артикул не выбран, сечение дано по габаритам из данных (ширина и глубина ниши, щель под свет), изделие подбирается по ним.

1000 мм · печать 1:1

Изм.	Кол.уч	Лист	№ док.	Подп.	Дата
Разраб.		Кырлан А.С.			04.11.26
Пров.					
ГИП					
Н. контр.					
Утв.					

ГД-2026-010-АИ

Дом 331 м²

Общая площадь 270,67* м² · * размеры приняты, не замерены (реестр — л. 8–10, К-1)

Дизайн-проект интерьера

Стадия	Лист	Листов
РП	79	216

Сечения потолков М 1:10

М 1:10

Кырлан Александр Сергеевич


выпуск 04.11.2026 № 2a77323a49 · стр. 81 из 221

Сечения потолков М 1:10

Пом. 5, 13, 19, 16 · профили, подвесы, крепёж, изделия · размеры в мм

Сечение 5.1. Короб с LED-подсветкой, теневой шов (М 1:10)


Пом. 5 Гостиная; карниз 150×100, щель под свет 60 мм

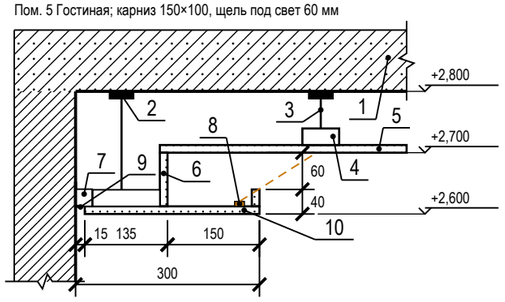

1 — плита перекрытия
2 — анкер-клин к плите — по одному на подвес
3 — подвес прямой, шаг 1000 мм
4 — ПП 60×27: несущие через 500, основные через 1200 мм; соединители одноуровневые, шурупы LN 3,5×9
5 — ГКЛ 12,5 по П113 — верхний уровень; шурупы TN 3,5×25 через 170 мм
6 — задняя стенка и бортик карниза — ГКЛ 12,5
7 — ПН 28×27 по периметру — дюбель-гвоздь через ≤ 500 мм, не менее 3 на профиль
8 — LED-лента 9,6 Вт/м, 24 В в алюминиевом профиле
9 — теневой профиль: шов 15 мм, зазор 3 мм
10 — низ короба — ГКЛ 12,5 по ПП 60×27

Сечение 5.2. Ниша под шторы (М 1:10)


Пом. 5 Гостиная; без подсветки; закладные под карниз — до обшивки

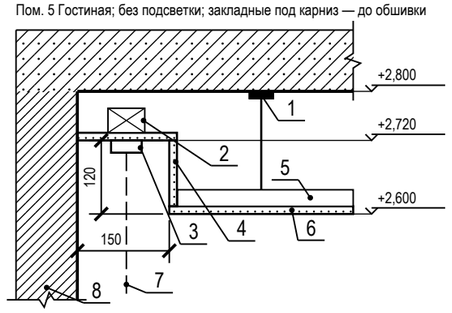

1 — анкер-клин к плите — по одному на подвес; подвес прямой, шаг 1000 мм
2 — закладная под карниз — брус 40×50
3 — карниз (шина), высота с верхом портьеры 100 мм
4 — стенка и потолок ниши — ГКЛ 12,5
5 — ПП 60×27 — каркас короба, основные через 1200 мм; соединители одноуровневые, шурупы LN 3,5×9
6 — низ короба нижнего уровня — ГКЛ 12,5; шурупы TN 3,5×25 через 170 мм
7 — портьера
8 — стена с окном

Сечение 13.1. Короб с LED-подсветкой (М 1:10)


Пом. 13 Спальня мастер, 19 Спальня 4; карниз 150×100, щель под свет 60 мм

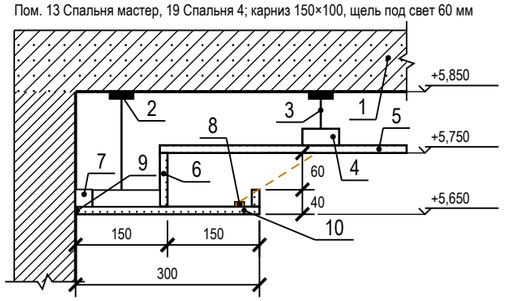

1 — плита перекрытия
2 — анкер-клин к плите — по одному на подвес
3 — подвес прямой, шаг 1000 мм
4 — ПП 60×27: несущие через 500, основные через 1200 мм; соединители одноуровневые, шурупы LN 3,5×9
5 — ГКЛ 12,5 по П113 — верхний уровень; шурупы TN 3,5×25 через 170 мм
6 — задняя стенка и бортик карниза — ГКЛ 12,5
7 — ПН 28×27 по периметру — дюбель-гвоздь через ≤ 500 мм, не менее 3 на профиль
8 — LED-лента 9,6 Вт/м, 24 В в алюминиевом профиле
9 — примыкание к стене — лента разделительная, шов зашпаклёван
10 — низ короба — ГКЛ 12,5 по ПП 60×27

Сечение 13.2. Примыкание потолка к стене (М 1:10)


Пом. 13 Спальня мастер, 19 Спальня 4; примыкание — разделительная лента

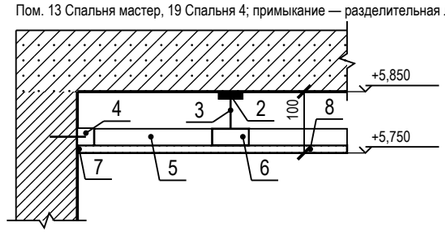

1 — плита перекрытия
2 — анкер-клин к плите — по одному на подвес
3 — подвес прямой, шаг 1000 мм
4 — ПН 28×27 по периметру — дюбель-гвоздь через ≤ 500 мм, не менее 3 на профиль
5 — ПП 60×27 несущий (вид) через 500 мм, в ПН
6 — ПП 60×27 основной (сечение) через 1200 мм; соединители одноуровневые, шурупы LN 3,5×9
7 — лента разделительная по стене, шов зашпаклёван
8 — ГКЛ 12,5 по П113; шурупы TN 3,5×25 через 170 мм

Сечение 16.1. Ниша LED фигурного уровня (М 1:10)


Пом. 16 Спальня 2; карниз 120×100, щель под свет 60 мм

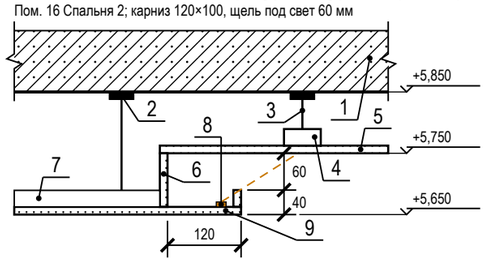

1 — плита перекрытия
2 — анкер-клин к плите — по одному на подвес
3 — подвес прямой, шаг 1000 мм
4 — ПП 60×27: несущие через 500, основные через 1200 мм; соединители одноуровневые, шурупы LN 3,5×9
5 — ГКЛ 12,5 по П113 — верхний уровень; шурупы TN 3,5×25 через 170 мм
6 — задняя стенка и бортик карниза — ГКЛ 12,5
7 — ПП 60×27 каркаса нижнего уровня, ПН по контуру фигуры (на дуге — с надрезами)
8 — LED-лента 9,6 Вт/м, 24 В в алюминиевом профиле
9 — низ короба — ГКЛ 12,5 по ПП 60×27

Сечение 16.2. Ниша под шторы (М 1:10)

Пом. 16 Спальня 2; без подсветки; закладные под карниз — до обшивки

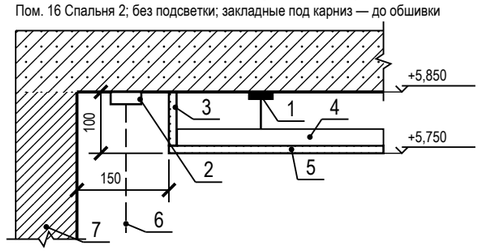

1 — анкер-клин к плите — по одному на подвес; подвес прямой, шаг 1000 мм
2 — карниз (шина), высота с верхом портьеры 100 мм
3 — стенка ниши — ГКЛ 12,5
4 — ПП 60×27 — каркас короба, основные через 1200 мм; соединители одноуровневые, шурупы LN 3,5×9
5 — низ короба нижнего уровня — ГКЛ 12,5; шурупы TN 3,5×25 через 170 мм
6 — портьера
7 — стена с окном

Условные обозначения

— · — LED-лента в нише подсветки (карниз короба, ниша фигуры)

Допущения и предложения на листе

Основа листа: размеры и контуры этажей подобраны проектировщиком по составу помещений и площадям этажей с картинки 470 px (размеры на ней не читаются); обмер и исходный проект — задание (К-1); высоты: 1-й этаж 2800 мм, мансарда 2700 мм (горизонтальная часть) приняты; скаты кровли мансарды приняты по картинке: колено 1200 мм, уклон 45°, конёк вдоль длинной стороны; проект КР — задание (К-2); наружные стены 400 мм, перегородки 120 мм приняты (К-1); разрешённая мощность 15 кВт принята по типовым ТУ для частного дома (К-4); подрайон климата не задан — принят не северный (жилые от 2,5 м) (К-7).
См. лист открытых вопросов (лист 8, записи К-1, К-2, К-4, К-7).

Примечания

1. Сечения потолков М 1:10 по помещениям с нишами LED и нишами под шторы: отметки и размеры этого помещения от ±0,000 — чистого пола 1-го этажа (м, мм). Положение — по плану потолков (листы 73, 74): короб и ниша LED — по линиям ленты, ниша под шторы — у стены с окном; типовые узлы по группам помещений — на листе 75.
2. Крепёж: подвес прямой к плите на анкер-клине — по одному на подвес (Knauf П113); ПН к стенам — дюбель-гвоздь через ≤ 500 мм, не менее 3 на профиль (серия 1.045.9-2.08); лист 12,5 — шурупы TN 3,5×25 через 170 мм (СП 163, табл. 15); профили между собой — соединители одноуровневые, шурупы LN 3,5×9.
3. Изделие карниза, профиля LED и галтели подписано артикулом из данных; где артикул не выбран, сечение дано по габаритам из данных (ширина и глубина ниши, щель под свет), изделие подбирается по ним.

1000 мм · печать 1:1

Изм.	Кол.уч	Лист	№ док.	Подп.	Дата
Разраб.		Кырлан А.С.			04.11.26
Пров.					
ГИП					
Н. контр.					
Утв.					

ГД-2026-010-АИ

Дом 331 м²

Общая площадь 270,67* м² · * размеры приняты, не замерены (реестр — л. 8–10, К-1)

Дизайн-проект интерьера

Стадия	Лист	Листов
РП	80	216

Сечения потолков М 1:10

М 1:10

Кырлан Александр Сергеевич


выпуск 04.11.2026 № 2a77323a49 · стр. 82 из 221

Сечения потолков М 1:10

Пом. 16, 18 · профили, подвесы, крепёж, изделия · размеры в мм

Сечение 16.3. Примыкание потолка к стене (М 1:10)


Пом. 16 Спальня 2; примыкание — теневой шов

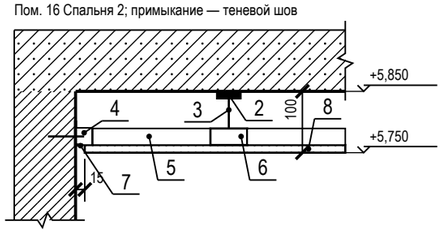

1 — плита перекрытия
2 — анкер-клин к плите — по одному на подвес
3 — подвес прямой, шаг 1000 мм
4 — ПН 28×27 по периметру — дюбель-гвоздь через ≤ 500 мм, не менее 3 на профиль
5 — ПП 60×27 несущий (вид) через 500 мм, в ПН
6 — ПП 60×27 основной (сечение) через 1200 мм; соединители одноуровневые, шурупы LN 3,5×9
7 — теневой профиль: шов 15 мм, зазор 3 мм; стена под шов выровнена
8 — ГКЛ 12,5 по П113; шурупы TN 3,5×25 через 170 мм

Сечение 18.1. Короб с LED-подсветкой, теневой шов (М 1:10)


Пом. 18 Спальня 3; карниз 150×100, щель под свет 60 мм

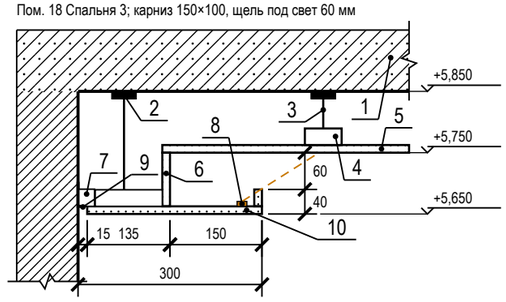

1 — плита перекрытия
2 — анкер-клин к плите — по одному на подвес
3 — подвес прямой, шаг 1000 мм
4 — ПП 60×27: несущие через 500, основные через 1200 мм; соединители одноуровневые, шурупы LN 3,5×9
5 — ГКЛ 12,5 по П113 — верхний уровень; шурупы TN 3,5×25 через 170 мм
6 — задняя стенка и бортик карниза — ГКЛ 12,5
7 — ПН 28×27 по периметру — дюбель-гвоздь через ≤ 500 мм, не менее 3 на профиль
8 — LED-лента 9,6 Вт/м, 24 В в алюминиевом профиле
9 — теневой профиль: шов 15 мм, зазор 3 мм
10 — низ короба — ГКЛ 12,5 по ПП 60×27

Сечение 18.2. Ниша под шторы (М 1:10)

Пом. 18 Спальня 3; без подсветки; закладные под карниз — до обшивки

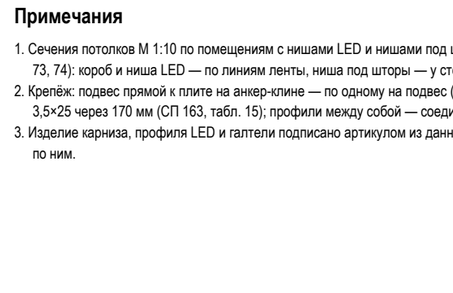

1 — анкер-клин к плите — по одному на подвес; подвес прямой, шаг 1000 мм
2 — закладная под карниз — брус 40×50
3 — карниз (шина), высота с верхом портьеры 100 мм
4 — стенка и потолок ниши — ГКЛ 12,5
5 — ПП 60×27 — каркас короба, основные через 1200 мм; соединители одноуровневые, шурупы LN 3,5×9
6 — низ короба нижнего уровня — ГКЛ 12,5; шурупы TN 3,5×25 через 170 мм
7 — портьера
8 — стена с окном

Условные обозначения

— · — LED-лента в нише подсветки (карниз короба, ниша фигуры)

Допущения и предложения на листе

Основа листа: размеры и контуры этажей подобраны проектировщиком по составу помещений и площадям этажей с картинки 470 px (размеры на ней не читаются); обмер и исходный проект — задание (К-1); высоты: 1-й этаж 2800 мм, мансарда 2700 мм (горизонтальная часть) приняты; скаты кровли мансарды приняты по картинке: колено 1200 мм, уклон 45°, конёк вдоль длинной стороны; проект КР — задание (К-2); наружные стены 400 мм, перегородки 120 мм приняты (К-1); разрешённая мощность 15 кВт принята по типовым ТУ для частного дома (К-4); подрайон климата не задан — принят не северный (жилые от 2,5 м) (К-7).
Знак «*» — принято, не замерено и не подтверждено (замерить на объекте): К-2: отметка чистого пола этажа «Мансарда» +3,150 — принята без источника, все отметки мансарды считаются от неё.
См. лист открытых вопросов (лист 8, записи К-1, К-2, К-4, К-7).

Примечания

1. Сечения потолков М 1:10 по помещениям с нишами LED и нишами под шторы: отметки и размеры этого помещения от ±0,000 — чистого пола 1-го этажа (м, мм). Положение — по плану потолков (листы 73, 74): короб и ниша LED — по линиям ленты, ниша под шторы — у стены с окном; типовые узлы по группам помещений — на листе 75.
2. Крепёж: подвес прямой к плите на анкер-клине — по одному на подвес (Knauf П113); ПН к стенам — дюбель-гвоздь через ≤ 500 мм, не менее 3 на профиль (серия 1.045.9-2.08); лист 12,5 — шурупы TN 3,5×25 через 170 мм (СП 163, табл. 15); профили между собой — соединители одноуровневые, шурупы LN 3,5×9.
3. Изделие карниза, профиля LED и галтели подписано артикулом из данных; где артикул не выбран, сечение дано по габаритам из данных (ширина и глубина ниши, щель под свет), изделие подбирается по ним.

1000 мм · печать 1:1

Изм.	Кол.уч	Лист	№ док.	Подп.	Дата
Разраб.		Кырлан А.С.			04.11.26
Пров.					
ГИП					
Н. контр.					
Утв.					

ГД-2026-010-АИ

Дом 331 м²

Общая площадь 270,67* м² · * размеры приняты, не замерены (реестр — л. 8–10, К-1)

Дизайн-проект интерьера

Стадия	Лист	Листов
РП	81	216

Сечения потолков М 1:10

М 1:10


Кырлан Александр Сергеевич

выпуск 04.11.2026 № 2a77323a49 · стр. 83 из 221


Раскладка плитки. Планы полов

Раскладка от чистовых размеров · размеры в мм · отметки от ±0,000 (чистый пол 1-го этажа)


Фрагмент 1. Санузел 1 этажа (пом. 3). Пол 600×600, шов 2 мм, М 1:50

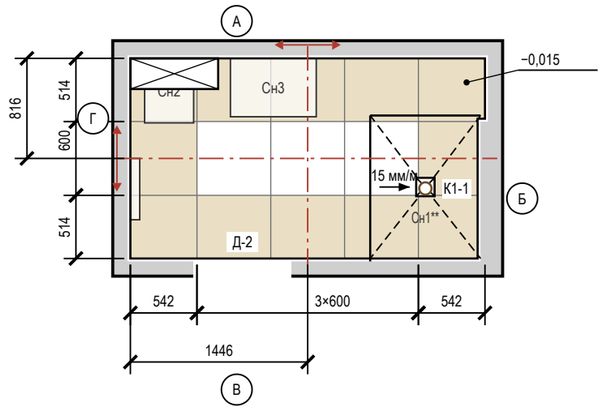

Фрагмент 2. Санузел мастер (пом. 15). Пол 600×600, шов 2 мм, М 1:50

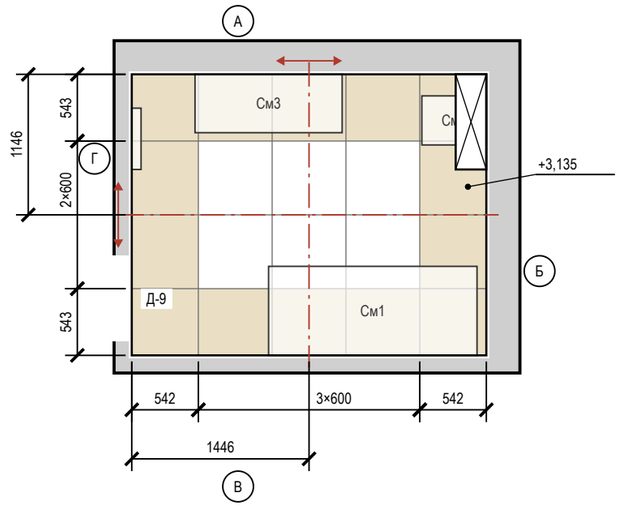

Фрагмент 3. Санузел 2 (пом. 20). Пол 600×600, шов 2 мм, М 1:50

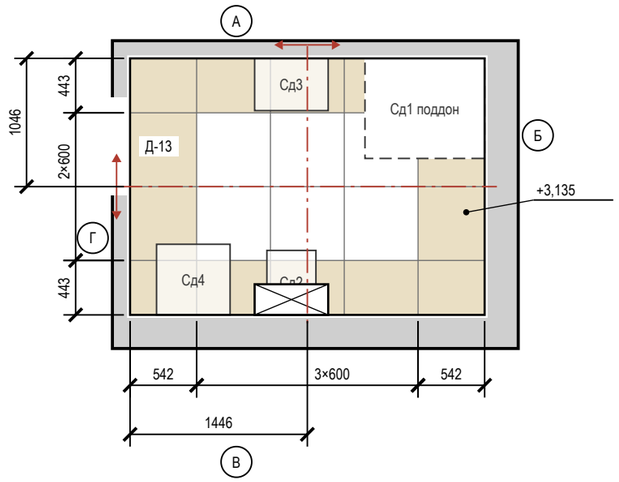

Допущения и предложения на листе

Основа листа: размеры и контуры этажей подобраны проектировщиком по составу помещений и площадям этажей с картинки 470 px (размеры на ней не читаются); обмер и исходный проект — задание (К-1); высоты: 1-й этаж 2800 мм, мансарда 2700 мм (горизонтальная часть) приняты; скаты кровли мансарды приняты по картинке: колено 1200 мм, уклон 45°, конёк вдоль длинной стороны; проект КР — задание (К-2); наружные стены 400 мм, перегородки 120 мм приняты (К-1); разрешённая мощность 15 кВт принята по типовым ТУ для частного дома (К-4); подрайон климата не задан — принят не северный (жилые от 2,5 м) (К-7).

Знак «**» — предложение проектировщика, заказчиком не утверждено (согласовать с заказчиком): пол пом. 3, 15, 20 — пирог пола: стяжка 33 мм и обмазочная гидроизоляция добавлены разработчиком проекта; артикул изделия не выбран: позиция описана характеристиками («аналог по характеристикам»), артикул выбирается при закупке; К-8: Сн1 — Подиум душевой зоны 100 мм — предложение проектировщика: трап в стяжке 35 мм не встаёт (монтажная высота трапа 90 + уклон отвода до стояка 42 = 132 мм).

См. лист открытых вопросов (лист 8, записи К-1, К-2, К-4, К-7; лист 9, запись К-8).

Ведомость материалов

Материал	Класс, код	Норма расхода	Кол-во
Затирка	CG2WA Mapei Ultracolor Plus 132	(a+b)/ab·шов·t·1,6	7,1 кг
Затирка	CG2WA	(a+b)/ab·шов·t·1,6	3,9 кг
Клей	C2 TE S1 Ceresit CM 17	1,5 кг/м²·мм, слой 5	691 кг (28 меш.)
Клей	C2 TE S1	1,5 кг/м²·мм, слой 5	389 кг (16 меш.)
Гидроизоляция	обмазочная, 2 слоя: пол, стены по периметру и зоны замачивания	по ТУ	44,9 м²
Демпф. лента	по периметру пола из плитки		90,5 м

Ведомость плитки

Помещение, поверхность	Плитка, код	Формат	Шов	S, м²	Целых	Подр.	С запасом
Санузел 1 этажа, пол	аналог: керамогранит под травертин	600×600	2	4,87	3	14	19
Санузел 1 этажа, стены А–Г	A8UZ	600×1200	2	19,67	11	19	34
Санузел 1 этажа, короб инсталляции	A8UZ	600×1200	2	1,64	0	6	7
Санузел мастер, пол	аналог: керамогранит под травертин	600×600	2	6,88	6	14	22
Санузел мастер, стены А–Г	A8UZ	600×1200	2	19,01	14	21	39
Санузел мастер, короб инсталляции	A8UZ	600×1200	2	1,73	0	6	7
Санузел 2, пол	аналог: керамогранит под травертин	600×600	2	6,29	5	14	21
Санузел 2, стены А–Г	A8UZ	600×1200	2	17,04	14	21	39
Санузел 2, короб инсталляции	A8UZ	600×1200	2	1,47	1	3	5
Котельная, пол	A8UZ	600×1200	2	6,88	0	10	11
Прихожая, пол	A8UZ	600×1200	2	12,46	3	16	21
Тамбур, пол	A8UZ	600×1200	2	3,49	0	6	7
Веранда, пол	A8UZ	600×1200	2	21,84	13	32	50
Крыльцо, пол	A8UZ	600×1200	2	3,38	0	6	7
Итого 600×600				18,04	14	42	62
Итого 600×1200				**108,60**	**56**	**146**	**227**

Условные обозначения

- плитка целая; тонкая линия — шов
- плитка с подрезкой (размер — на цепочке)
- ось старта; стрелки — направление укладки
- сантехприбор: габарит, высота по практике
- поддон душа — плитку пола под ним не кладут
- короб инсталляции: плитка пола — до короба
- трап / лоток в полу
- направление уклона К1 / пола: Ø, мм на 1 м
- край подиума; штрих — конверт к трапу
- вывод К1 (код — в ведомости привязок)
- отметка чистого пола на полке выноски, м
- А — обозначение стены А–Г (как на развёртках)

1000 мм · печать 1:1

Примечания

1. Раскладка от чистовых размеров: стены санузлов теряют 10 + 5 + 9 = 24 мм на сторону (штукатурка, клей, плитка); подрезки — чистые, без шва.
2. Старт — от центра помещения (штрихпунктир, стрелки — направление укладки); размер старта — от чистовых стен Г и А.
3. Раскладка пола «Котельная» и пола «Прихожая» и пола «Тамбур» и пола «Веранда» и пола «Крыльцо» — на листе «Раскладка плитки. Котельная. Прихожая. Тамбур. Веранда. Крыльцо».
4. Калибр партии не задан — до укладки замерить (рабочий размер W, ГОСТ 13996-2019) и пересчитать подрезки.
5. Количество: целые по раскладке + по одной на подрезку, запас 10 %; один артикул — одна партия и тон. Исключены поддон, короб, проёмы и места за коробом; S — по чистым граням: стены нетто = зона облицовки по ведомости отделки − место за коробом инсталляции 2,51 м² (плитку за коробом не кладут), короб — отдельной строкой.
6. Клей C2 TE S1 Ceresit CM 17; C2 TE S1 (ГОСТ Р 56387-2018), затирка CG2WA Mapei Ultracolor Plus 132; CG2WA; расход — по ТУ выбранной марки.
7. Гидроизоляция: пол и стены 200 мм от ЧП; у душа — на всю высоту стен душевой зоны и 500 мм за край душевой зоны (пом. 3), над ванной — до 2000 и 300 мм за борт (пом. 15), у душа до 2000 и 500 мм за поддон (пом. 20) (см. развёртки); акт скрытых работ, пролив 24 ч.
8. Подиум душа Сн1** (пом. 3): h 100 у трапа, решётка +0,085; верх — плиткой пола той же раскладки, уклон 15 мм/м к трапу, подрезка по линиям конверта; ступень по краю 109, грань 900 × 109 + 1166 × 107 = 0,22 м² (+2 шт. в подрезках), угол — профилем; гидроизоляция 2 сл. — по плите под подиумом, по верху и грани (узел 1 ВК); предложение, до согласования не выполнять.
9. Швы пола совмещены со швами стены А; по периметру — демпферная лента.
10. Отметка чистого пола −0,015, +3,135, порог 15 мм; стык с соседним покрытием — по оси полотна двери.

Изм.	Кол.уч	Лист	№ док.	Подп.	Дата
Разраб.		Кырлан А.С.			04.11.26
Пров.					
ГИП					
Н. контр.					
Утв.					

ГД-2026-010-АИ

Дом 331 м²

Общая площадь 270,67* м² · * размеры приняты, не замерены (реестр — л. 8–10, К-1)

Дизайн-проект интерьера

Стадия	Лист	Листов
РП	82	216

Раскладка плитки. Планы полов

М 1:50


Кырлан Александр Сергеевич

выпуск 04.11.2026 № 2a77323a49 · стр. 84 из 221


Раскладка плитки. Котельная. Прихожая. Тамбур

Раскладка от чистовых размеров · размеры в мм · высоты фартука от чистого пола


Фрагмент 1. Котельная (пом. 4). Пол 600×1200, шов 2 мм, М 1:40

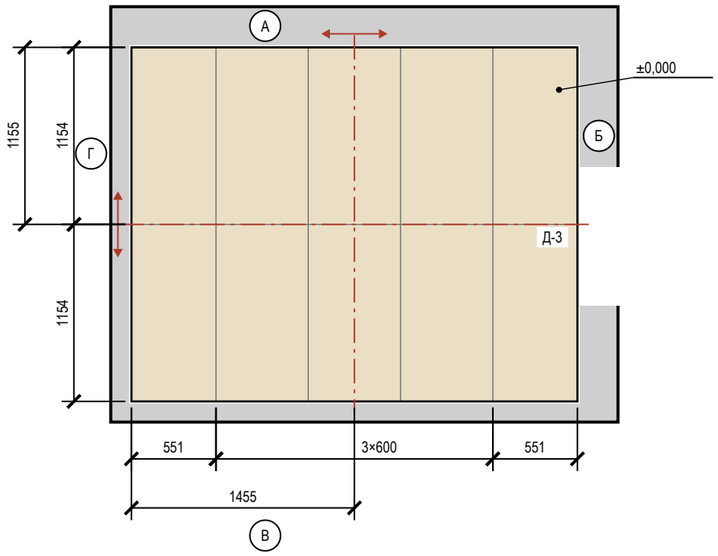

Фрагмент 2. Прихожая (пом. 8). Пол 600×1200, шов 2 мм, М 1:40

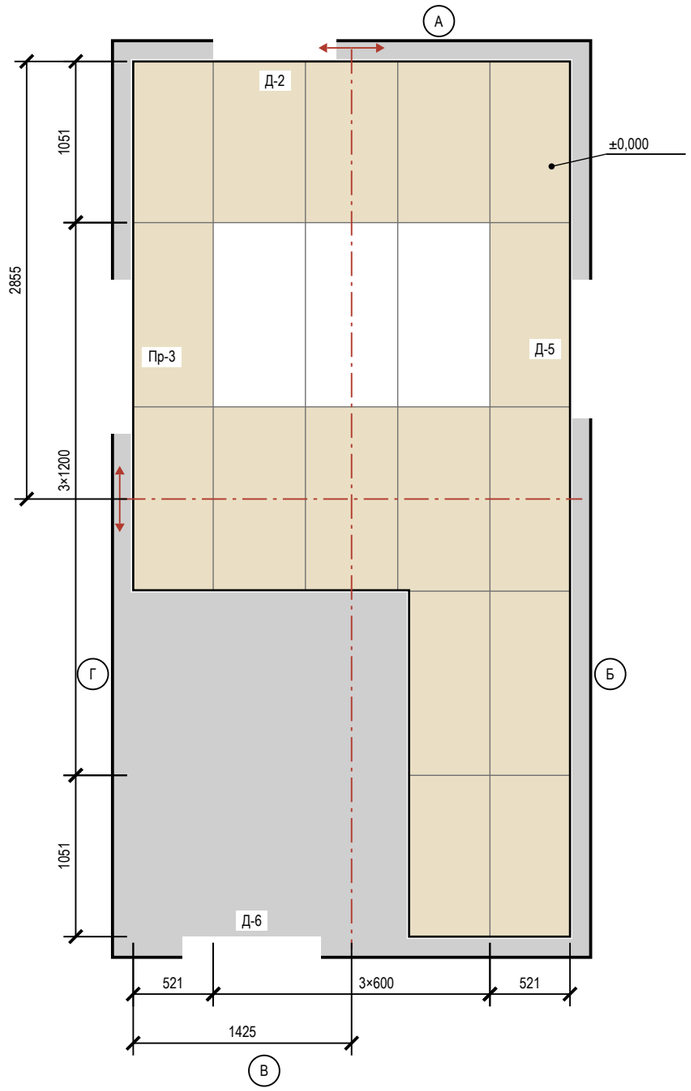

Фрагмент 3. Тамбур (пом. 9). Пол 600×1200, шов 2 мм, М 1:40

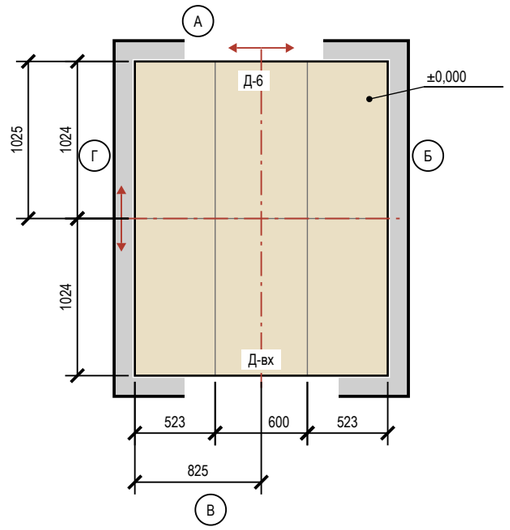

Подсчёт плитки

Поверхность	Формат	S, м²	Целых	Подр.	С запасом
Котельная, пол	600×1200	6,88	0	10	11
Прихожая, пол	600×1200	12,46	3	16	21
Тамбур, пол	600×1200	3,49	0	6	7

Условные обозначения

- плитка целая; тонкая линия — шов
- плитка с подрезкой (размер — на цепочке)
- ось старта; стрелки — направление укладки
- отметка чистого пола на полке выноски, м
- (А) обозначение стены А–Г (как на развёртках)

Допущения и предложения на листе

Основа листа: размеры и контуры этажей подобраны проектировщиком по составу помещений и площадям этажей с картинки 470 px (размеры на ней не читаются); обмер и исходный проект — задание (К-1); высоты: 1-й этаж 2800 мм, мансарда 2700 мм (горизонтальная часть) приняты; скаты кровли мансарды приняты по картинке: колено 1200 мм, уклон 45°, конёк вдоль длинной стороны; проект КР — задание (К-2); наружные стены 400 мм, перегородки 120 мм приняты (К-1); разрешённая мощность 15 кВт принята по типовым ТУ для частного дома (К-4); подрайон климата не задан — принят не северный (жилые от 2,5 м) (К-7).
Знак «**» — предложение проектировщика, заказчиком не утверждено (согласовать с заказчиком): плинтус пом. 4, 8, 9 — артикул изделия не выбран: позиция описана характеристиками («аналог по характеристикам»), артикул выбирается при закупке.
См. лист открытых вопросов (лист 8, записи К-1, К-2, К-4, К-7).

Примечания

1. Котельная: керамогранит 600×1200, длинная сторона — вдоль стен Б и Г, шов 2 мм, прямая раскладка от центра. Стены окрашены: раскладка от чистового контура минус штукатурка и шпаклёвка 15 мм на сторону (принято); подрезки 551 / 1154 мм, срез — под плинтус.
2. Котельная: деформационный зазор по периметру 8–10 мм под плинтусом; в проёмах — стык с соседним покрытием по оси полотна двери. Клей С2 TE S1, затирка CG2WA.
3. Прихожая: керамогранит 600×1200, длинная сторона — вдоль стен Б и Г, шов 2 мм, прямая раскладка от центра. Стены окрашены: раскладка от чистового контура минус штукатурка и шпаклёвка 15 мм на сторону (принято); подрезки 521 / 1051 мм, срез — под плинтус.
4. Прихожая: деформационный зазор по периметру 8–10 мм под плинтусом; в проёмах — стык с соседним покрытием по оси полотна двери. Клей С2 TE S1, затирка CG2WA.
5. Тамбур: керамогранит 600×1200, длинная сторона — вдоль стен Б и Г, шов 2 мм, прямая раскладка от центра. Стены окрашены: раскладка от чистового контура минус штукатурка и шпаклёвка 15 мм на сторону (принято); подрезки 523 / 1024 мм, срез — под плинтус.
6. Тамбур: деформационный зазор по периметру 8–10 мм под плинтусом; в проёмах — стык с соседним покрытием по оси полотна двери. Клей С2 TE S1, затирка CG2WA.
7. Клей, затирка и итог по форматам — в ведомостях листа «Раскладка плитки. Планы полов».

1000 мм · печать 1:1

Изм.	Кол.уч	Лист	№ док.	Подп.	Дата
Разраб.		Кырлан А.С.			04.11.26
Пров.					
ГИП					
Н. контр.					
Утв.					

ГД-2026-010-АИ

Дом 331 м²

Общая площадь 270,67* м² · * размеры приняты, не замерены (реестр — л. 8–10, К-1)

Дизайн-проект интерьера

Стадия	Лист	Листов
РП	83	216

Раскладка плитки. Котельная. Прихожая. Тамбур

М 1:40


Кырлан Александр Сергеевич

выпуск 04.11.2026 № 2a77323a49 · стр. 85 из 221


Раскладка плитки. Веранда. Крыльцо

Раскладка от чистовых размеров · размеры в мм · высоты фартука от чистого пола

Фрагмент 1. Веранда (пом. 11). Пол 600×1200, шов 2 мм, М 1:40

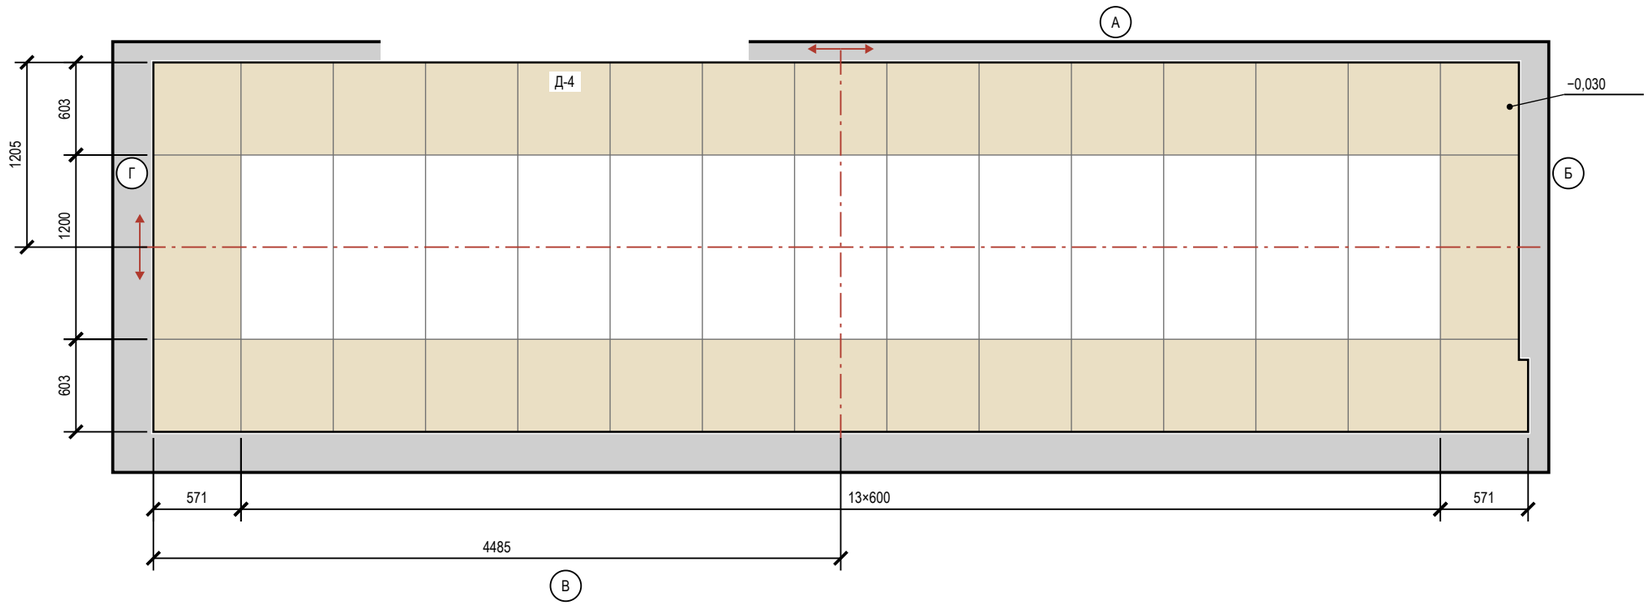

Фрагмент 2. Крыльцо (пом. 12). Пол 600×1200, шов 2 мм, М 1:40

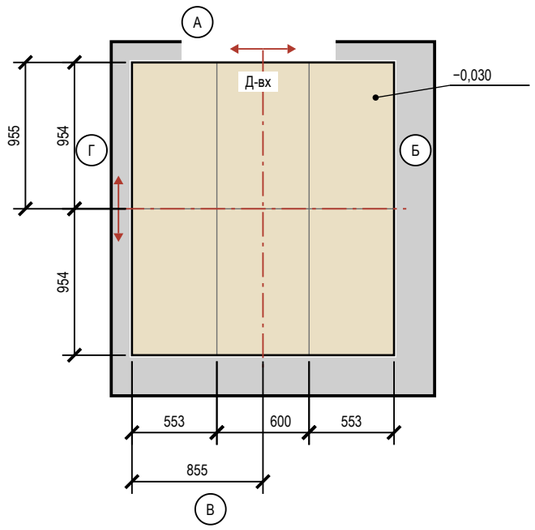

Условные обозначения

- плитка целая; тонкая линия — шов
- плитка с подрезкой (размер — на цепочке)
- ось старта; стрелки — направление укладки
- отметка чистого пола на полке выноски, м
- (А) обозначение стены А–Г (как на развёртках)

Подсчёт плитки

Поверхность	Формат	S, м²	Целых	Подр.	С запасом
Веранда, пол	600×1200	21,84	13	32	50
Крыльцо, пол	600×1200	3,38	0	6	7

Примечания

1. Веранда: керамогранит 600×1200, длинная сторона — вдоль стен Б и Г, шов 2 мм, прямая раскладка от центра. Стены окрашены: раскладка от чистового контура минус штукатурка и шпаклёвка 15 мм на сторону (принято); подрезки 571 / 603 мм, срез — под плинтус.
2. Веранда: деформационный зазор по периметру 8–10 мм под плинтусом; в проёмах — стык с соседним покрытием по оси полотна двери. Клей С2 TE S1, затирка CG2WA.
3. Крыльцо: керамогранит 600×1200, длинная сторона — вдоль стен Б и Г, шов 2 мм, прямая раскладка от центра. Стены окрашены: раскладка от чистового контура минус штукатурка и шпаклёвка 15 мм на сторону (принято); подрезки 553 / 954 мм, срез — под плинтус.
4. Крыльцо: деформационный зазор по периметру 8–10 мм под плинтусом; в проёмах — стык с соседним покрытием по оси полотна двери. Клей С2 TE S1, затирка CG2WA.
5. Клей, затирка и итог по форматам — в ведомостях листа «Раскладка плитки. Планы полов».

Допущения и предложения на листе

Основа листа: размеры и контуры этажей подобраны проектировщиком по составу помещений и площадям этажей с картинки 470 px (размеры на ней не читаются); обмер и исходный проект — задание (К-1); высоты: 1-й этаж 2800 мм, мансарда 2700 мм (горизонтальная часть) приняты; скаты кровли мансарды приняты по картинке: колено 1200 мм, уклон 45°, конёк вдоль длинной стороны; проект КР — задание (К-2); наружные стены 400 мм, перегородки 120 мм приняты (К-1); разрешённая мощность 15 кВт принята по типовым ТУ для частного дома (К-4); подрайон климата не задан — принят не северный (жилые от 2,5 м) (К-7).

Знак «*» — принято, не замерено и не подтверждено (замерить на объекте): К-13: пол пом. 11, 12 — отметка верха плиты −0,170 принята по пирогу (плита веранды и крыльца своя, ниже плиты дома) — подтвердить по проекту КР или обмером (К-13).

Знак «**» — предложение проектировщика, заказчиком не утверждено (согласовать с заказчиком): плинтус пом. 11, 12 — артикул изделия не выбран: позиция описана характеристиками («аналог по характеристикам»), артикул выбирается при закупке.

См. лист открытых вопросов (лист 8, записи К-1, К-2, К-4, К-7; лист 9, запись К-13).

1000 мм · печать 1:1

Изм.	Кол.уч	Лист	№ док.	Подп.	Дата
Разраб.		Кырлан А.С.			04.11.26
Пров.					
ГИП					
Н. контр.					
Утв.					

ГД-2026-010-АИ

Дом 331 м²

Общая площадь 270,67* м² · * размеры приняты, не замерены (реестр — л. 8–10, К-1)

Дизайн-проект интерьера

Стадия	Лист	Листов
РП	84	216

Раскладка плитки. Веранда. Крыльцо

М 1:40


Кырлан Александр Сергеевич

выпуск 04.11.2026 № 2a77323a49 · стр. 86 из 221

Раскладка плитки. Санузел 1 этажа. Развёртки стен

ПРЕДВАРИТЕЛЬНО · не для производства работ · открыто пунктов: 15 (реестр — л. 8–10)

Пом. 3 · вид изнутри помещения · размеры в мм · высоты от чистого пола, отметки от ±0,000 (чистый пол 1-го этажа)

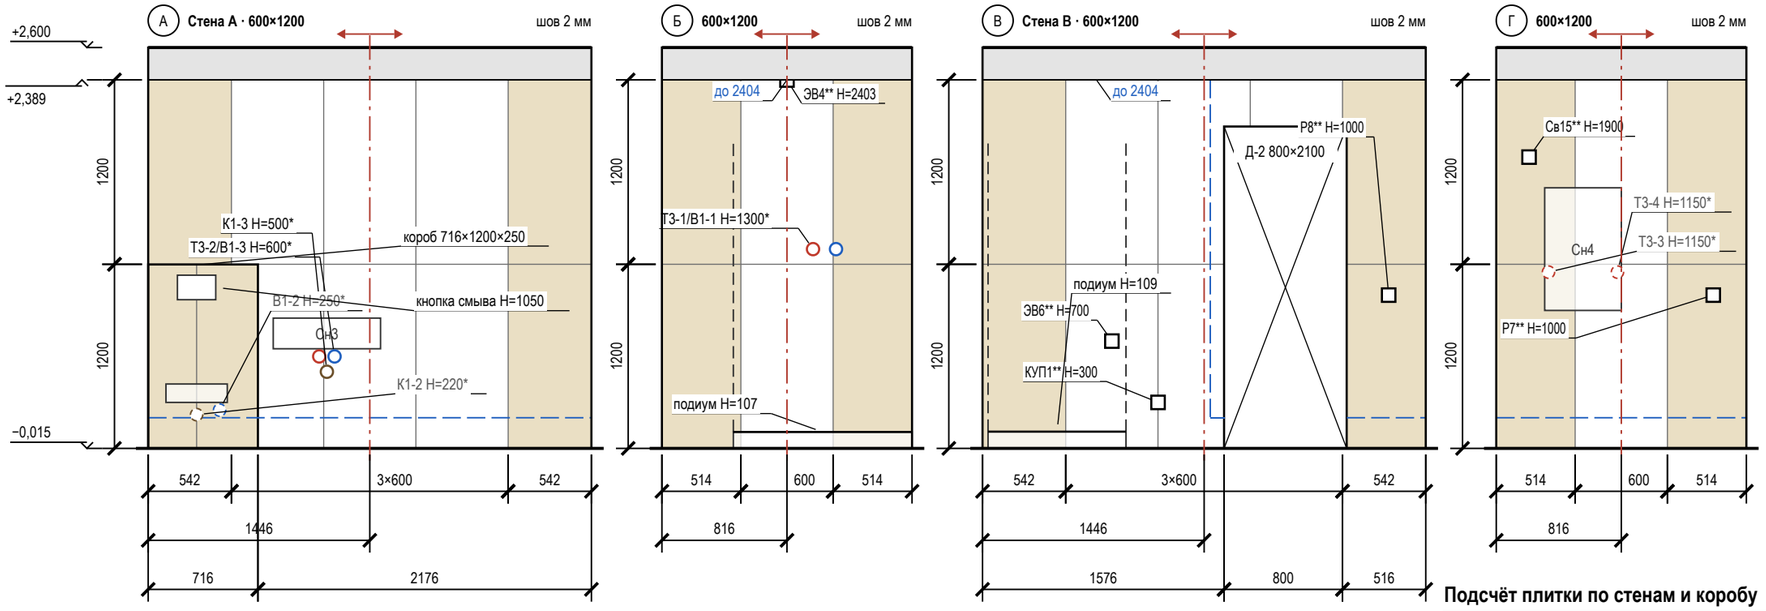

Условные обозначения

- плитка целая; тонкая линия — шов
- плитка с подрезкой (размер — на цепочке)
- ось старта; стрелки — направление укладки
- верх гидроизоляции: 200 от ЧП, в мокрой зоне — «до …»
- проём — не облицовывается
- сантехприбор: габарит, высота по практике
- граница душевой зоны (ограждение)
- короб инсталляции, в нём кнопка смыва 250×160
- вывод В1 (код — в ведомости привязок)
- вывод Т3 (код — в ведомости привязок)
- вывод К1 (код — в ведомости привязок)
- вывод за прибором / в коробе (не на сетке)
- электроточка: марка и Н — по листам ЭОМ
- отметка уровня, м: ±0,000 — чистый пол 1-го этажа
- низ потолка; серая полоса — стена без плитки
- А — обозначение стены А–Г (как на развёртках)

Примечания

1. Вид изнутри, стены по часовой стрелке А → Г. Высоты — от чистого пола (−0,015), отметки — от ±0,000 (чистый пол 1-го этажа). Раскладка от чистовых размеров (штукатурка 10 + клей 5 + плитка 9 мм), подрезки чистые; старт — от оси стены, ряды от пола целыми.
2. Облицовка не до потолка: верх плитки +2,389, выше — отделка стены по ведомости отделки до потолка +2,600; торец облицовки — профиль-окантовка.
3. Открытые выводы и электроточки — на шве или в центре плитки (допуск 10 мм; плитка от 900 мм по высоте на шве или не ближе 60 мм к нему).
4. Выводы ВК стоят по оси прибора и с прибором не двигаются — привязки по «Плану выводов сантехники» без сдвига; вне сетки (Т3-2/В1-3, К1-3, Т3-1/В1-1) — отверстие в плитке коронкой по той же привязке, плитку не сдвигать.
5. Выводы — по «Плану выводов сантехники», электроточки — по ЭОМ, «*» — высота по практике; за приборами и в коробе (В1-2, К1-2, Т3-3, Т3-4) — штриховым кольцом.
6. Подиум душа Сн1**: верх у решётки трапа +0,085 (h 100 мм), к стенам поднимается уклоном к трапу — «подиум Н=…» на развёртке — верх подиума у этой стены; облицовка стен в зоне душа — от верха подиума, грань ступени — плиткой пола. Выводы В1-1, Т3-1: Н=1300 от чистого пола помещения = 1200 от верха подиума у трапа.
7. Гидроизоляция: 200 мм от ЧП по периметру; у душа — на всю высоту стен душевой зоны и 500 мм за край душевой зоны (СП 29.13330.2011, п. 7.2 — на высоту замачивания); углы — лентой; акт скрытых работ, пролив.
8. Короб 716×1200×250: лицо 315 / 399 мм от оси кнопки смыва, боковины, полка; углы — запил 45° или профиль; за коробом плитку не кладут.

Подсчёт плитки по стенам и коробу

Поверхность	L × H, мм	S, м²	Целых	Подр.	С запасом	Подрезки: край / верх, мм
стена А	2892 × 2404	6,21	5	4	10	542 / 542; целый ряд
короб (ст. А)	716×1200×250	1,64	0	6	7	лицо 315 / 399; бок. 250
стена Б	1632 × 2404	4,04	2	4	7	514 / 514; целый ряд
стена В	2892 × 2404	5,39	2	7	10	542 / 542; целый ряд
стена Г	1632 × 2404	4,04	2	4	7	514 / 514; целый ряд
Итого		**21,31**	**11**	**25**	**41**	

Допущения и предложения на листе. Основа листа: размеры и контуры этажей подобраны проектировщиком по составу помещений и площадям этажей с картинки 470 px (размеры на ней не читаются); обмер и исходный проект — задание (К-1); высоты: 1-й этаж 2800 мм, мансарда 2700 мм (горизонтальная часть) приняты; скаты кровли мансарды приняты по картинке: колено 1200 мм, уклон 45°, конёк вдоль длинной стороны; проект КР — задание (К-2); наружные стены 400 мм, перегородки 120 мм приняты (К-1); разрешённая мощность 15 кВт принята по типовым ТУ для частного дома (К-4); подрайон климата не задан — принят не северный (жилые от 2,5 м) (К-7). Знак «**» — предложено, не утверждено (согласовать): пол пом. 3, Р7, Р8, Св15, ЭВ4, КУП1, ЭВ6; К-8: Сн1. См. лист открытых вопросов (лист 8, записи К-1, К-2, К-4, К-7; лист 9, запись К-8).

1000 мм · печать 1:1

Изм.	Кол.уч	Лист	№ док.	Подп.	Дата
Разраб.		Кырлан А.С.			04.11.26
Пров.					
ГИП					
Н. контр.					
Утв.					

ГД-2026-010-АИ

Дом 331 м²

Общая площадь 270,67* м² · * размеры приняты, не замерены (реестр — л. 8–10, К-1)

Дизайн-проект интерьера

Стадия	Лист	Листов
РП	85	216

Раскладка плитки. Санузел 1 этажа. Развёртки стен

М 1:40


Кырлан Александр Сергеевич

выпуск 04.11.2026 № 2a77323a49 · стр. 87 из 221

Раскладка плитки. Санузел мастер. Развёртки стен

ПРЕДВАРИТЕЛЬНО · не для производства работ · открыто пунктов: 15 (реестр — л. 8–10)

Пом. 15 · вид изнутри помещения · размеры в мм · высоты от чистого пола, отметки от ±0,000 (чистый пол 1-го этажа)

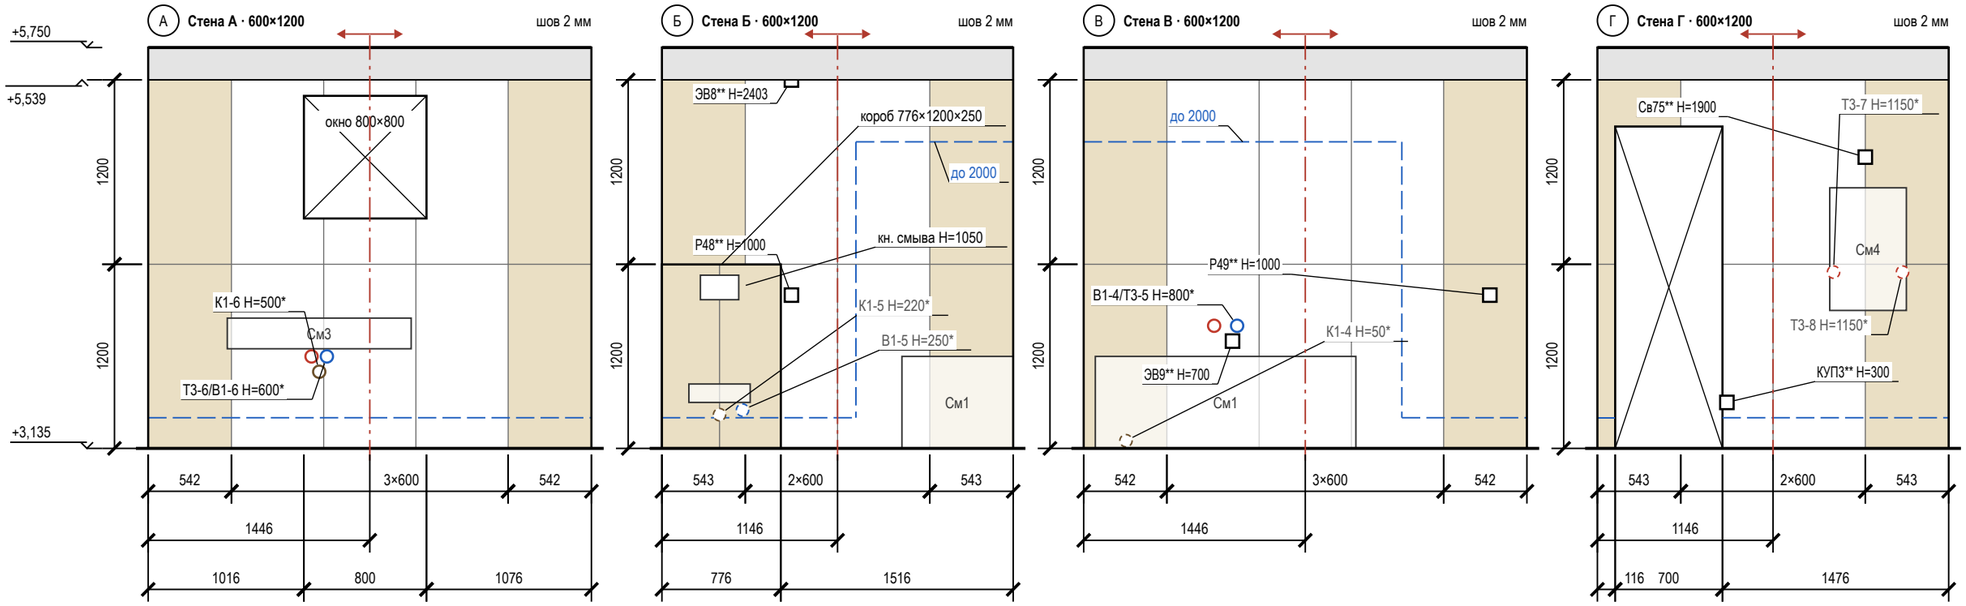

Подсчёт плитки по стенам и коробу

Поверхность	L × H, мм	S, м²	Целых	Подр.	С запасом	Подрезки: край / верх, мм
стена А	2892 × 2404	4,54	3	7	11	542 / 542; целый ряд
стена Б	2292 × 2404	3,97	3	4	8	543 / 543; целый ряд
короб (ст. Б)	776×1200×250	1,73	0	6	7	лицо 375 / 399; бок. 250
стена В	2892 × 2404	7,07	6	4	11	542 / 542; целый ряд
стена Г	2292 × 2404	3,43	2	6	9	543 / 543; целый ряд
Итого		**20,73**	**14**	**27**	**46**	

Сдвиг точек под раскладку

Точка (ВК, ЭОМ)	Стена	Проект: от угла / Н	Под раскладку: от угла / Н	Сдвиг, мм
ЭВ9**	В	971 / 700	844 / 700	−127 в центр плитки

Условные обозначения

- плитка целая; тонкая линия — шов
- плитка с подрезкой (размер — на цепочке)
- ось старта; стрелки — направление укладки
- верх гидроизоляции: 200 от ЧП, в мокрой зоне — «до …»
- проём — не облицовывается
- сантехприбор: габарит, высота по практике
- короб инсталляции, в нём кнопка смыва 250×160
- вывод В1 (код — в ведомости привязок)
- вывод Т3 (код — в ведомости привязок)
- вывод К1 (код — в ведомости привязок)
- вывод за прибором / в коробе (не на сетке)
- электроточка: марка и Н — по листам ЭОМ
- отметка уровня, м: ±0,000 — чистый пол 1-го этажа
- низ потолка; серая полоса — стена без плитки
- А — обозначение стены А–Г (как на развёртках)

Примечания

1. Вид изнутри, стены по часовой стрелке А → Г. Высоты — от чистого пола (+3,135), отметки — от ±0,000 (чистый пол 1-го этажа). Раскладка от чистовых размеров (штукатурка 10 + клей 5 + плитка 9 мм), подрезки чистые; старт — от оси стены, ряды от пола целыми.
2. Облицовка не до потолка: верх плитки +5,539, выше — отделка стены по ведомости отделки до потолка +5,750; торец облицовки — профиль-окантовка.
3. Точки из таблицы сдвигов переносятся до черновой разводки (ЭОМ — по тем же числам).
4. Выводы ВК стоят по оси прибора и с прибором не двигаются — привязки по «Плану выводов сантехники» без сдвига; вне сетки (Т3-6/В1-6, К1-6, В1-4/Т3-5) — отверстие в плитке коронкой по той же привязке, плитку не сдвигать.
5. Выводы — по «Плану выводов сантехники», электроточки — по ЭОМ, «*» — высота по практике; за приборами и в коробе (В1-5, К1-5, К1-4, Т3-7, Т3-8) — штриховым кольцом.
6. Гидроизоляция: 200 мм от ЧП по периметру; над ванной — до 2000 и 300 мм за борт (СП 29.13330.2011, п. 7.2 — на высоту замачивания); углы — лентой; акт скрытых работ, пролив.
7. Короб 776×1200×250: лицо 375 / 399 мм от оси кнопки смыва, боковины, полка; углы — запил 45° или профиль; за коробом плитку не кладут.

Допущения и предложения на листе. Основа листа: размеры и контуры этажей подобраны проектировщиком по составу помещений и площадям этажей с картинки 470 px (размеры на ней не читаются); обмер и исходный проект — задание (К-1); высоты: 1-й этаж 2800 мм, мансарда 2700 мм (горизонтальная часть) приняты; скаты кровли мансарды приняты по картинке: колено 1200 мм, уклон 45°, конёк вдоль длинной стороны; проект КР — задание (К-2); наружные стены 400 мм, перегородки 120 мм приняты (К-1); разрешённая мощность 15 кВт принята по типовым ТУ для частного дома (К-4); подрайон климата не задан — принят не северный (жилые от 2,5 м) (К-7). Знак «*» — принято, не замерено (замерить): К-2: отметка чистого пола этажа «Мансарда» +3,150. Знак «**» — предложено, не утверждено (согласовать): пол пом. 15, ЭВ9, Р48, Р49, Св75, ЭВ8, КУП3. См. лист открытых вопросов (лист 8, записи К-1, К-2, К-4, К-7).

1000 мм · печать 1:1

Изм.	Кол.уч	Лист	№ док.	Подп.	Дата
Разраб.		Кырлан А.С.			04.11.26
Пров.					
ГИП					
Н. контр.					
Утв.					

ГД-2026-010-АИ

Дом 331 м²

Общая площадь 270,67* м² · * размеры приняты, не замерены (реестр — л. 8–10, К-1)

Дизайн-проект интерьера

Стадия	Лист	Листов
РП	86	216

Раскладка плитки. Санузел мастер. Развёртки стен

М 1:40


Кырлан Александр Сергеевич

выпуск 04.11.2026 № 2a77323a49 · стр. 88 из 221

Раскладка плитки. Санузел 2. Развёртки стен

ПРЕДВАРИТЕЛЬНО · не для производства работ · открыто пунктов: 15 (реестр — л. 8–10)

Пом. 20 · вид изнутри помещения · размеры в мм · высоты от чистого пола, отметки от ±0,000 (чистый пол 1-го этажа)

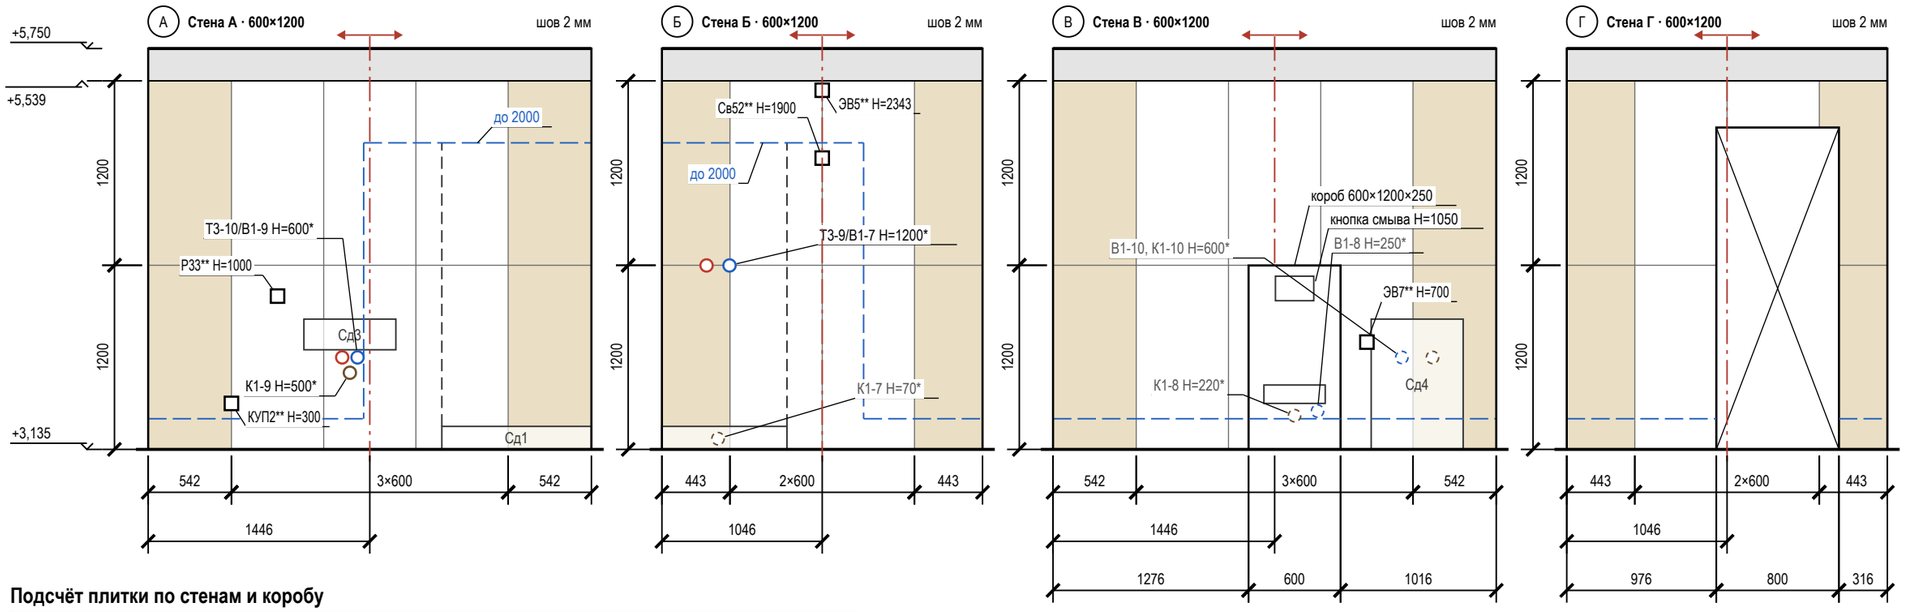

Подсчёт плитки по стенам и коробу

Поверхность	L × H, мм	S, м²	Целых	Подр.	С запасом	Подрезки: край / верх, мм
стена А	2892 × 2404	7,07	6	4	11	542 / 542; целый ряд
стена Б	2092 × 2404	4,42	4	4	9	443 / 443; целый ряд
стена В	2892 × 2404	2,81	4	6	11	542 / 542; целый ряд
короб (ст. В)	600×1200×250	1,47	1	3	5	лицо 600; бок. 250
стена Г	2092 × 2404	2,74	0	7	8	443 / 443; целый ряд
Итого		**18,51**	**15**	**24**	**44**	

Условные обозначения

- плитка целая; тонкая линия — шов
- плитка с подрезкой (размер — на цепочке)
- ось старта; стрелки — направление укладки
- верх гидроизоляции: 200 от ЧП, в мокрой зоне — «до …»
- проём — не облицовывается
- сантехприбор: габарит, высота по практике
- граница душевой зоны (ограждение)
- короб инсталляции, в нём кнопка смыва 250×160
- вывод В1 (код — в ведомости привязок)
- вывод Т3 (код — в ведомости привязок)
- вывод К1 (код — в ведомости привязок)
- вывод за прибором / в коробе (не на сетке)
- электроточка: марка и Н — по листам ЭОМ
- отметка уровня, м: ±0,000 — чистый пол 1-го этажа
- низ потолка; серая полоса — стена без плитки
- (А) обозначение стены А–Г (как на развёртках)

Примечания

1. Вид изнутри, стены по часовой стрелке А → Г. Высоты — от чистого пола (+3,135), отметки — от ±0,000 (чистый пол 1-го этажа). Раскладка от чистовых размеров (штукатурка 10 + клей 5 + плитка 9 мм), подрезки чистые; старт — от оси стены, ряды от пола целыми.
2. Облицовка не до потолка: верх плитки +5,539, выше — отделка стены по ведомости отделки до потолка +5,750; торец облицовки — профиль-окантовка.
3. Открытые выводы и электроточки — на шве или в центре плитки (допуск 10 мм; плитка от 900 мм по высоте — на шве или не ближе 60 мм к нему).
4. Выводы ВК стоят по оси прибора и с прибором не двигаются — привязки по «Плану выводов сантехники» без сдвига; вне сетки (Т3-10/В1-9, К1-9, Т3-9/В1-7) — отверстие в плитке коронкой по той же привязке, плитку не сдвигать.
5. Выводы — по «Плану выводов сантехники», электроточки — по ЭОМ, «*» — высота по практике; за приборами и в коробе (К1-7, В1-8, К1-8, В1-10, К1-10) — штриховым кольцом.
6. Гидроизоляция: 200 мм от ЧП по периметру; у душа — до 2000 и 500 мм за поддон (СП 29.13330.2011, п. 7.2 — на высоту замачивания); углы — лентой; акт скрытых работ, пролив.
7. Короб 600×1200×250: лицо 600 мм от оси кнопки смыва, боковины, полка; углы — запил 45° или профиль; за коробом плитку не кладут.

Допущения и предложения на листе. Основа листа: размеры и контуры этажей подобраны проектировщиком по составу помещений и площадям этажей с картинки 470 px (размеры на ней не читаются); обмер и исходный проект — задание (К-1); высоты: 1-й этаж 2800 мм, мансарда 2700 мм (горизонтальная часть) приняты; скаты кровли мансарды приняты по картинке: колено 1200 мм, уклон 45°, конёк вдоль длинной стороны; проект КР — задание (К-2); наружные стены 400 мм, перегородки 120 мм приняты (К-1); разрешённая мощность 15 кВт принята по типовым ТУ для частного дома (К-4); подрайон климата не задан — принят не северный (жилые от 2,5 м) (К-7). Знак «*» — принято, не замерено (замерить): К-2: отметка чистого пола этажа «Мансарда» +3,150. Знак «**» — предложено, не утверждено (согласовать): пол пом. 20, Р33, КУП2, ЭВ7; ИЗ-1: Св52, ЭВ5. См. лист открытых вопросов (лист 8, записи К-1, К-2, К-4, К-7; лист 10, запись ИЗ-1).

1000 мм · печать 1:1

Изм.	Кол.уч	Лист	№ док.	Подп.	Дата
Разраб.		Кырлан А.С.			04.11.26
Пров.					
ГИП					
Н. контр.					
Утв.					

ГД-2026-010-АИ

Дом 331 м²

Общая площадь 270,67* м² · * размеры приняты, не замерены (реестр — л. 8–10, К-1)

Дизайн-проект интерьера

Стадия	Лист	Листов
РП	87	216

Раскладка плитки. Санузел 2. Развёртки стен


М 1:40

Кырлан Александр Сергеевич

выпуск 04.11.2026 № 2a77323a49 · стр. 89 из 221

План полов · 1-й этаж

Покрытия, направление укладки, отметки чистого пола, стыки · размеры в мм · отметки в м

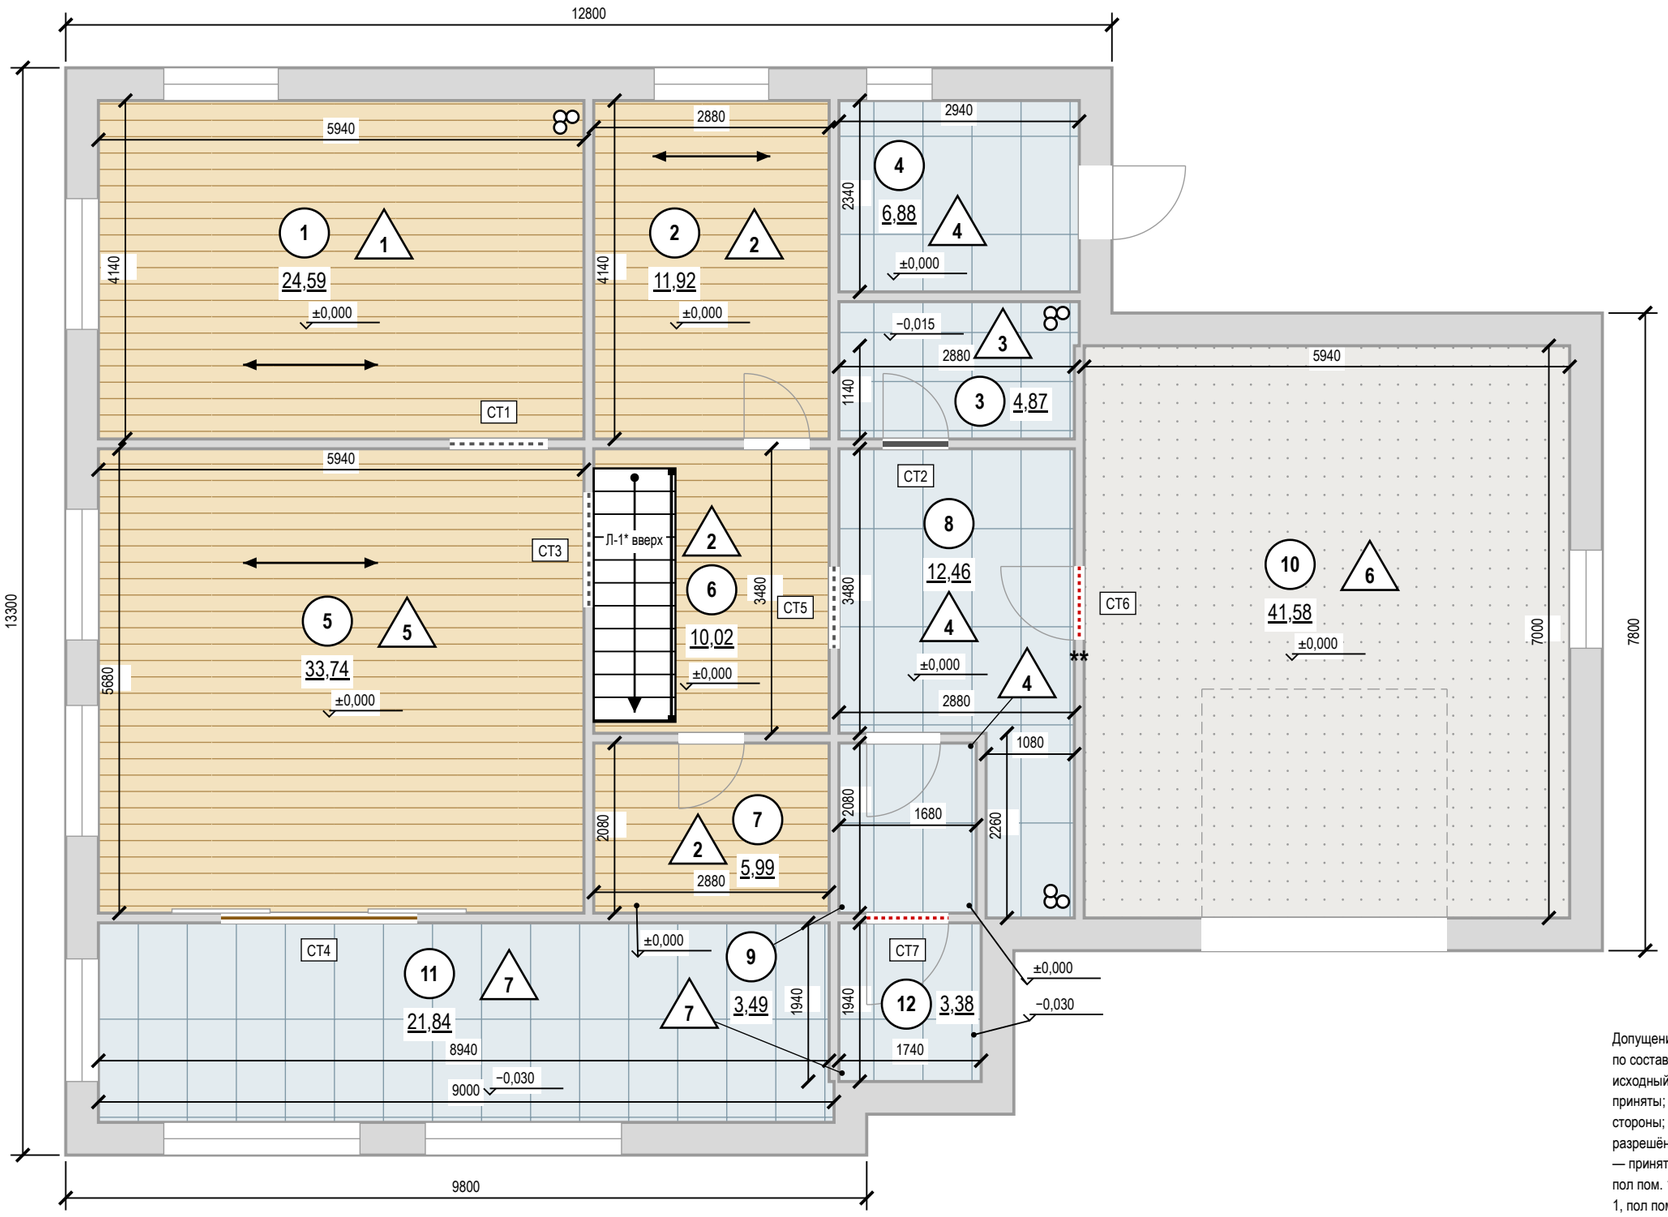

Условные обозначения

- тип 1 — инженерная доска, линии — вдоль доски
- тип 2 — инженерная доска, линии — вдоль доски
- тип 3 — керамогранит 600×600, сетка — формат плитки
- тип 4 — керамогранит 600×1200, сетка — формат плитки
- тип 5 — инженерная доска, линии — вдоль доски
- тип 6 — наливной пол
- тип 7 — керамогранит 600×1200, сетка — формат плитки
- 1 — номер типа пола (экспликация полов)
- схема пола, без масштаба: плита — штриховка, стяжка — точки, звукоизоляция — зигзаг, гидроизоляция — утолщённая линия с заведением на стену
- направление укладки (длинная сторона доски)
- отметка чистого пола, м
- стык в проёме: без порога (б/п)
- стык в проёме: порог
- стык в проёме: Т-профиль по оси полотна
- стык в проёме: решение не задано
- CT1 — марка стыка (ведомость стыков)
- стояк: К1 — канализация, В1 — ХВС, Т3 — ГВС
- 1 — номер помещения, площадь м²

Отметки по высоте

±0,000	чистый пол пом. 1, 2, 4–10; отсчёт высот
−0,015	чистый пол пом. 3, ниже на 15 мм
−0,030	чистый пол пом. 11, 12, ниже на 30 мм
плита*	верх плиты разный: −0,064, −0,170 (задание на обмер)
сущ. пол	снимается до плиты; не замерен (задание на обмер)

Допущения и предложения на листе. Основа листа: размеры и контуры этажей подобраны проектировщиком по составу помещений и площадям этажей с картинки 470 px (размеры на ней не читаются); обмер и исходный проект — задание (К-1); высоты: 1-й этаж 2800 мм, мансарда 2700 мм (горизонтальная часть) приняты; скаты кровли мансарды приняты по картинке: колено 1200 мм, уклон 45°, конёк вдоль длинной стороны; проект КР — задание (К-2); наружные стены 400 мм, перегородки 120 мм приняты (К-1); разрешённая мощность 15 кВт принята по типовым ТУ для частного дома (К-4); подрайон климата не задан — принят не северный (жилые от 2,5 м) (К-7). Знак «*» — принято, не замерено (замерить): К-6: Л-1; К-13: пол пом. 11, 12. Знак «**» — предложено, не утверждено (согласовать): плинтус пом. 1, 2, 4–12, фартук пом. 1, пол пом. 3, 10, акцент пом. 5; К-9: дверь пом. 5 (стена В). См. лист открытых вопросов (лист 8, записи К-1, К-2, К-4, К-6, К-7; лист 9, записи К-8, К-9, К-13).

Примечания

1. За отметку ±0,000 принят чистый пол 1-го этажа, не существующий (блок отметок). Площади — по чистым размерам помещений, м²; размеры — в мм.
2. Стык разнотипных покрытий — по оси дверного полотна (под полотном в закрытом положении); решение стыка — по ведомости стыков.
3. Размеры помещений в свету (ширина × длина, мм), не поместившиеся на плане: пом. 3 — 2940 × 540, 2880 × 1140; пом. 6 — 2880 × 3480.
4. Пол санузлов ниже смежных помещений на 15 мм; гидроизоляция по стяжке с заведением на стены не менее 200 мм (СП 29.13330.2011, п. 7.2), до облицовки — тест проливом и акт скрытых работ.
5. Трубопроводы в конструкции пола не прокладываются: пирог пола 49–140 мм не вмещает выпуски канализации с уклоном — выпуски К1 ведутся по стенам над чистым полом в коробах.
6. Штучные покрытия (инженерная доска): направление — по стрелке; влажность основания по СМ не более 2,0 % (по ТУ изготовителя).
7. Ровность основания — просвет под 2-метровой рейкой не более 2 мм: пом. 1, 2, 5, 6, 7 (инженерная доска), пом. 3, 4, 8, 9 (керамогранит), пом. 10 (наливной пол); 3 мм: пом. 11, 12 (керамогранит); проверить до укладки покрытия (СП 71.13330.2017, табл. 8.5).
8. Сетка на плитке — условная, в размер формата; точка старта и раскладка — по листу раскладки плитки.
9. Узор покрытия (заливка-код типа пола) прерывается под надписями — площадями помещений и отметками чистого пола.
10. Пироги полов — по экспликации полов: слои сверху вниз, толщины в мм; гидроизоляция мокрых зон — в пироге и в ведомости отделки; схема пола — без масштаба.
11. Экспликация полов (ф. 4 прил. А ГОСТ 21.501-2018) и ведомость стыков покрытий — на отдельном листе 90.

1000 мм · печать 1:1

Изм.	Кол.уч	Лист	№ док.	Подп.	Дата
Разраб.		Кырлан А.С.			04.11.26
Пров.					
ГИП					
Н. контр.					
Утв.					

ГД-2026-010-АИ

Дом 331 м²

Общая площадь 270,67* м² · * размеры приняты, не замерены (реестр — л. 8–10, К-1)

Дизайн-проект интерьера

Стадия	Лист	Листов
РП	88	216

План полов · 1-й этаж

М 1:75

Кырлан Александр Сергеевич

выпуск 04.11.2026 № 2a77323a49 · стр. 90 из 221


План полов · Мансарда

Покрытия, направление укладки, отметки чистого пола, стыки · размеры в мм · отметки в м

ПРЕДВАРИТЕЛЬНО · не для производства работ · открыто пунктов: 15 (реестр — л. 8–10)

Условные обозначения

- тип 1 — инженерная доска, линии — вдоль доски
- тип 2 — керамогранит 600×600, сетка — формат плитки
- 1 — номер типа пола (экспликация полов)
- схема пола, без масштаба: плита — штриховка, стяжка — точки, звукоизоляция — зигзаг, гидроизоляция — утолщённая линия с заведением на стену
- направление укладки (длинная сторона доски)
- отметка чистого пола, м
- стык в проёме: порог
- СТ1 — марка стыка (ведомость стыков)
- стояк: К1 — канализация, В1 ХВС, Т3 — ГВС
- 1 — номер помещения, площадь м²

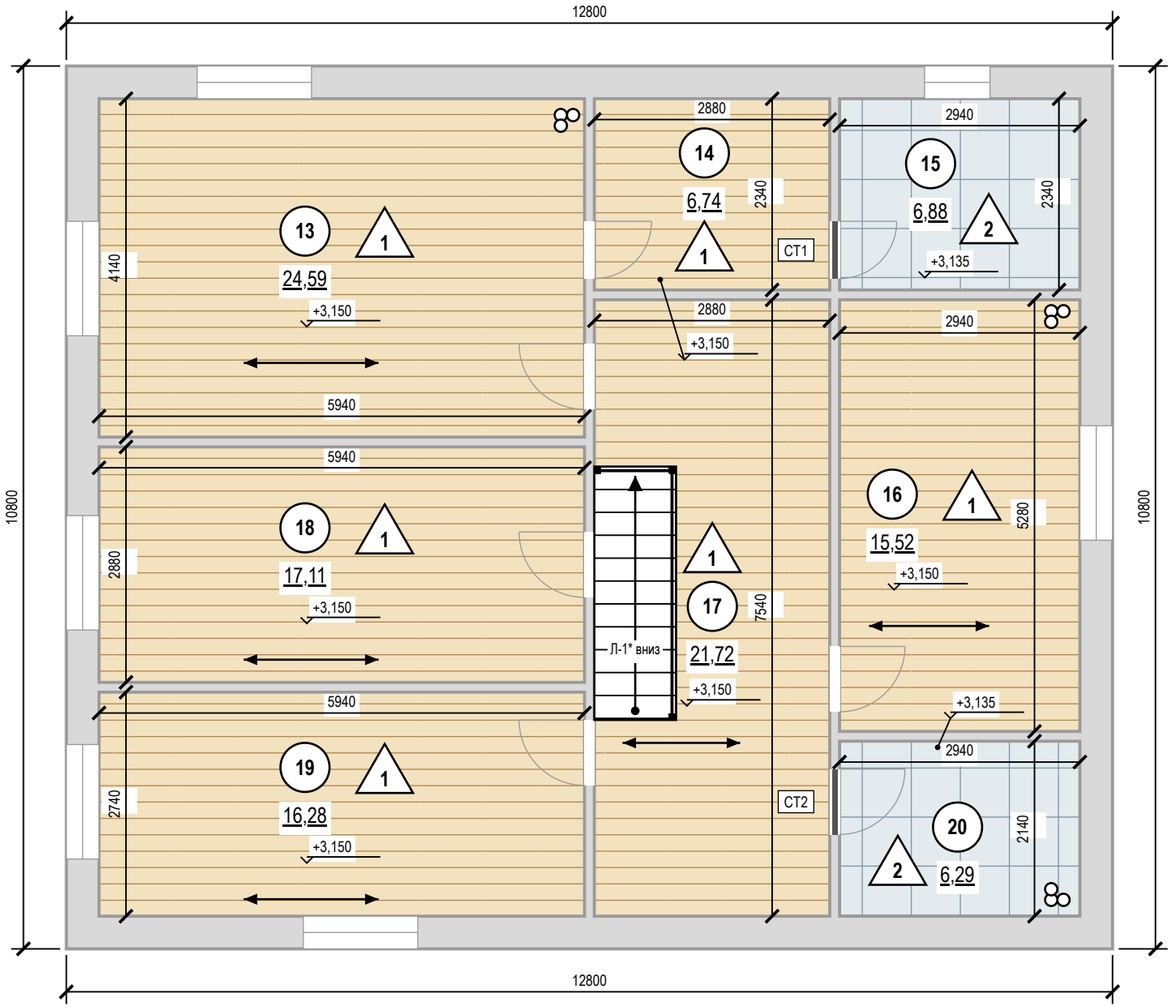

Допущения и предложения на листе

Основа листа: размеры и контуры этажей подобраны проектировщиком по составу помещений и площадям этажей с картинки 470 px (размеры на ней не читаются); обмер и исходный проект — задание (К-1); высоты: 1-й этаж 2800 мм, мансарда 2700 мм (горизонтальная часть) приняты; скаты кровли мансарды приняты по картинке: колено 1200 мм, уклон 45°, конёк вдоль длинной стороны; проект КР — задание (К-2); наружные стены 400 мм, перегородки 120 мм приняты (К-1); разрешённая мощность 15 кВт принята по типовым ТУ для частного дома (К-4); подрайон климата не задан — принят не северный (жилые от 2,5 м) (К-7).



Знак «*» — принято, не замерено и не подтверждено (замерить на объекте): К-2: отметка чистого пола этажа «Мансарда» +3,150 — принята без источника, все отметки мансарды считаются от неё; К-6: Л-1 — габарит марша снят с картинки заказчика (11 проступей в холле 3,6 м), а до отм. +3,150 нужно 18 подъёмов — одномаршевая не встаёт: решение по К-6.

Знак «**» — предложение проектировщика, заказчиком не утверждено (согласовать с заказчиком): плинтус пом. 13, 14, 16, 17 — артикул изделия не выбран: позиция описана характеристиками («аналог по характеристикам»), артикул выбирается при закупке; пол пом. 15, 20 — пирог пола: стяжка 33 мм и обмазочная гидроизоляция добавлены разработчиком проекта; артикул изделия не выбран: позиция описана характеристиками («аналог по характеристикам»), артикул выбирается при закупке.

Открытые вопросы и конфликты по листу: К-8, К-13.

См. лист открытых вопросов (лист 8, записи К-1, К-2, К-4, К-6, К-7; лист 9, записи К-8, К-13).

Экспликация полов

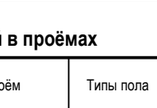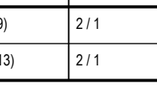Номер помещения	Тип пола	Схема пола	Данные элементов пола (наименование, толщина, основание), мм	Площадь, м²
13, 14, 16, 17, 18, 19	1		Инженерная доска на клею — 14 Стяжка ЦПС М200 — 50 Плита перекрытия Всего 64 мм; ЧП +3,150, верх плиты +3,086	101,96
15, 20	2		Керамогранит на клею С2 TE S1 — 14 Гидроизоляция обмазочная, 2 слоя, с заведением на стены 200 мм — 2 Стяжка ЦПС М200 — 33 Плита перекрытия Всего 49 мм; ЧП +3,135, верх плиты +3,086	13,17
			Итого	**115,13**

Раскладка покрытий

Пом.	Укладка	Старт (оси от чистовых стен), мм	Отступ 1-го ряда / крайние плитки, мм
13	вдоль стен А/В, прямая	от стены А, 1-й ряд вдоль неё	зазор от стены не задан
14	вдоль стен А/В, прямая	от стены А, 1-й ряд вдоль неё	зазор от стены не задан
15	прямая, сетка 600×600, шов 2	ось X 1446 от Г; ось Y 1146 от А	X 542 / 542; Y 543 / 543
16	вдоль стен А/В, прямая	от стены А, 1-й ряд вдоль неё	зазор от стены не задан
17	вдоль стен А/В, прямая	от стены А, 1-й ряд вдоль неё	зазор от стены не задан
18	вдоль стен А/В, прямая	от стены А, 1-й ряд вдоль неё	зазор от стены не задан
19	вдоль стен А/В, прямая	от стены В, 1-й ряд вдоль неё	зазор от стены не задан
20	прямая, сетка 600×600, шов 2	ось X 1446 от Г; ось Y 1046 от А	X 542 / 542; Y 443 / 443

Стыки покрытий в проёмах

Марка	Проём	Типы пола	Отметки ЧП	Решение
СТ1	15–14 (Д-9)	2 / 1	+3,135 / +3,150	порог h=15 мм
СТ2	20–17 (Д-13)	2 / 1	+3,135 / +3,150	порог h=15 мм

Отметки по высоте

±0,000 чистый пол 1-го этажа; отсчёт отметок
+3,150* чистый пол пом. 13, 14, 16–19 (мансарда)
+3,135* чистый пол пом. 15, 20, ниже на 15 мм
+3,086* верх плиты — расчёт, не замер (задание на обмер)
сущ. пол снимается до плиты; не замерен (задание на обмер)

Примечания

1. За отметку ±0,000 принят чистый пол 1-го этажа, не существующий; чистый пол этажа +3,150 (блок отметок). Площади — по чистым размерам помещений, м²; размеры — в мм.
2. Стык разнотипных покрытий — по оси дверного полотна (под полотном в закрытом положении); решение стыка — по ведомости стыков.
3. Пол санузлов ниже смежных помещений на 15 мм за счёт меньшей толщины стяжки (верх плиты общий — по экспликации полов); гидроизоляция по стяжке с заведением на стены не менее 200 мм (СП 29.13330.2011, п. 7.2), до облицовки — тест проливом и акт скрытых работ.
4. Трубопроводы в конструкции пола не прокладываются: пирог пола 49–64 мм не вмещает выпуски канализации с уклоном — выпуски К1 ведутся по стенам над чистым полом в коробах.
5. Штучные покрытия (инженерная доска): направление — по стрелке; влажность основания по СМ не более 2,0 % (по ТУ изготовителя).
6. Ровность основания — просвет под 2-метровой рейкой не более 2 мм: пом. 13, 14, 16, 17, 18, 19 (инженерная доска), пом. 15, 20 (керамогранит); проверить до укладки покрытия (СП 71.13330.2017, табл. 8.5).
7. Сетка на плитке — условная, в размер формата; точка старта и раскладка — по листу раскладки плитки.
8. Узор покрытия (заливка-код типа пола) прерывается под надписями — площадями помещений и отметками чистого пола.
9. Пироги полов — по экспликации полов: слои сверху вниз, толщины в мм; гидроизоляция мокрых зон — в пироге и в ведомости отделки; схема пола — без масштаба.

1000 мм · печать 1:1

Изм.	Кол.уч	Лист	№ док.	Подп.	Дата
Разраб.		Кырлан А.С.			04.11.26
Пров.					
ГИП					
Н. контр.					
Утв.					

ГД-2026-010-АИ

Дом 331 м²

Общая площадь 270,67* м² · * размеры приняты, не замерены (реестр — л. 8–10, К-1)

Дизайн-проект интерьера

Стадия	Лист	Листов
РП	89	216

План полов · Мансарда

М 1:75

Кырлан Александр Сергеевич







выпуск 04.11.2026 № 2a77323a49 · стр. 91 из 221

Конструкции полов и стыки покрытий

Форма 4 прил. А ГОСТ 21.501-2018 · толщины в мм · отметки в м

ПРЕДВАРИТЕЛЬНО · не для производства работ · открыто пунктов: 15 (реестр — л. 8–10)

Экспликация полов

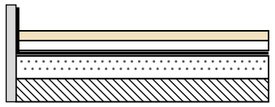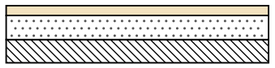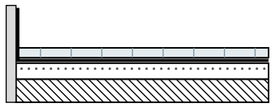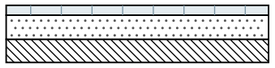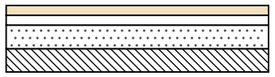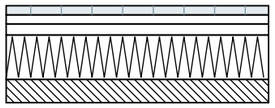Номер помещения	Тип пола	Схема пола	Данные элементов пола (наименование, толщина, основание), мм	Площадь, м²
1	1		Инженерная доска дуб на клею — 14 Клей паркетный МС-полимерный — 1 Гидроизоляция полиуретановая, 2 слоя (зона мойки и острова) — 2 Стяжка ЦПС М300 (В22,5), фибра, по звукоизоляции — 47 Плита перекрытия монолитная Всего 64 мм; ЧП ±0,000, верх плиты −0,064	24,59
2, 6, 7, 13, 14, 16, 17, 18, 19	2		Инженерная доска на клею — 14 Стяжка ЦПС М200 — 50 Плита перекрытия Всего 64 мм; ЧП ±0,000; +3,150	129,89
3, 15, 20	3		Керамогранит на клею С2 TE S1 — 14 Гидроизоляция обмазочная, 2 слоя, с заведением на стены 200 мм — 2 Стяжка ЦПС М200 — 33 Плита перекрытия Всего 49 мм; ЧП −0,015; +3,135	18,04
4, 8, 9	4		Керамогранит на клею С2 TE S1 — 14 Стяжка ЦПС М200 — 50 Плита перекрытия Всего 64 мм; ЧП ±0,000, верх плиты −0,064	22,83
5	5		Инженерная доска дуб на клею — 14 Клей паркетный МС-полимерный — 1 Стяжка ЦПС М300 (В22,5), фибра, по звукоизоляции — 49 Плита перекрытия монолитная Всего 64 мм; ЧП ±0,000, верх плиты −0,064	33,74
10	6		Наливной полимерный пол с грунтом и кварцевой посыпкой — 3 Стяжка ЦПС М300, армированная сеткой — 61 Плита перекрытия по грунту Всего 64 мм; ЧП ±0,000, верх плиты −0,064	41,58
11, 12	7		Керамогранит 600×600×10 — 10 Клей плиточный С2 TE S1 (деформируемый) — 5 Сборное основание ГВЛВ 2×12,5 — 25 Пенополистирол экструзионный 2×50 — 100 Плита перекрытия монолитная Всего 140 мм; ЧП −0,030, верх плиты −0,170	25,22
			Итого	**295,89**

Стыки покрытий в проёмах

Марка	Проём	Типы пола	Отметки ЧП	Решение
СТ1	1–5 (Пр-1)	1 / 5	±0,000 / ±0,000	б/п
СТ2	3–8 (Д-2)	3 / 4	−0,015 / ±0,000	порог h=15 мм
СТ3	5–6 (Пр-2)	5 / 2	±0,000 / ±0,000	б/п
СТ4	5–11 (Д-4)	5 / 7	±0,000 / −0,030	Т-профиль
СТ5	8–6 (Пр-3)	4 / 2	±0,000 / ±0,000	б/п
СТ6	8–10 (Д-5)	4 / 6	±0,000 / ±0,000	не задано
СТ7	9–12 (Д-вх)	4 / 7	±0,000 / −0,030	не задано
СТ8	15–14 (Д-9)	3 / 2	+3,135 / +3,150	порог h=15 мм
СТ9	20–17 (Д-13)	3 / 2	+3,135 / +3,150	порог h=15 мм

Условные обозначения

- схема пола, без масштаба: плита — штриховка, стяжка — точки, звукоизоляция — зигзаг, гидроизоляция — утолщённая линия с заведением на стену
- стык в проёме: без порога (б/п)
- стык в проёме: порог
- стык в проёме: Т-профиль по оси полотна
- стык в проёме: решение не задано
- СТ1 — марка стыка (ведомость стыков)

Примечания

1. Экспликация полов — по форме 4 прил. А ГОСТ 21.501-2018: слои пирога сверху вниз, толщины в мм; схема пола — без масштаба.
2. Номера помещений, площади, отметки чистого пола, направление укладки и места стыков — по листу «План полов»; привязка марок стыков (СТ) на плане полов, тип каждой схемы пола — в строке экспликации.
3. Стык разнотипных покрытий — по оси дверного полотна (под полотном в закрытом положении).
4. Гидроизоляция мокрых зон — с заведением на стены не менее 200 мм (СП 29.13330.2011, п. 7.2); до облицовки — тест проливом и акт скрытых работ.

Допущения и предложения на листе

Основа листа: размеры и контуры этажей подобраны проектировщиком по составу помещений и площадям этажей с картинки 470 px (размеры на ней не читаются); обмер и исходный проект — задание (К-1); высоты: 1-й этаж 2800 мм, мансарда 2700 мм (горизонтальная часть) приняты; скаты кровли мансарды приняты по картинке: колено 1200 мм, уклон 45°, конёк вдоль длинной стороны; проект КР — задание (К-2); наружные стены 400 мм, перегородки 120 мм приняты (К-1); разрешённая мощность 15 кВт принята по типовым ТУ для частного дома (К-4); подрайон климата не задан — принят не северный (жилые от 2,5 м) (К-7).
См. лист открытых вопросов (лист 8, записи К-1, К-2, К-4, К-7).

Изм.	Кол.уч	Лист	№ док.	Подп.	Дата
Разраб.		Кырлан А.С.			04.11.26
Пров.					
ГИП					
Н. контр.					
Утв.					

ГД-2026-010-АИ

Дом 331 м²

Общая площадь 270,67* м² · * размеры приняты, не замерены (реестр — л. 8–10, К-1)

Дизайн-проект интерьера

Стадия	Лист	Листов
РП	90	216

Конструкции полов и стыки покрытий

М б/м

Кырлан Александр Сергеевич

выпуск 04.11.2026 № 2a77323a49 · стр. 92 из 221

Ведомость отделки помещений. Лист 1 из 4

Потолки, стены, низ стен, полы · площади в м², длины в м · отметки в м

Ведомость отделки помещений (форма 1 прил. А ГОСТ 21.501-2018). Лист 1 из 4

№	Наименование помещения	Потолок			Стены и перегородки			Низ стен (плинтус)			Пол		Примечание
		Вид отделки	Код цвета	S, м²	Вид отделки	Код цвета	S, м²	Вид отделки	Код цвета	L, м	Вид отделки	S, м²	
1	Кухня-столовая 24,59 м²	ГКЛ по каркасу П113, отм. +2,700; +2,550; +2,600; окраска, Tikkurila Luja 7, матовая, 2 слоя, подготовка Q3	NCS S 0804-Y30R	24,59	Окраска, Tikkurila Luja 7, полуматовая, 2 слоя, подготовка К3 Фартук кухни (стена А): облицовка керамогранитом, аналог: керамогранит матовый, тон F497, 600×600×9 мм, клей C2 TE S1, затирка CG2WA	NCS S 0804-Y30R #F1F1EC	44,80 1,15	Плинтус МДФ h=80 мм, аналог: МДФ под окраску 80×16 мм	NCS S 0804-Y30R	18,3	Инженерная доска, 1167-4250, 2100×127 мм, на клею; тип 1, отм. ЧП ±0,000	24,59	Н стен 2700 (до потолка); влагостойкая полуматовая окраска (класс мокрого истирания 1 по EN 13300); категория К3 по СП 71.13330.2017, табл. 7.5; по ГКЛ каркаса П113, влагостойкая окраска; Q3 колеруется в код стен, но по эмали на МДФ: сличать отдельным выкрасом на своей подложке (выкрас № 10); плинтус в цвет: стены
2	Кабинет-гостевая 11,92 м²	ГКЛ по каркасу П113, отм. +2,700; +2,600; окраска, Little Greene Absolute Matt, глубокоматовая, 2 слоя, подготовка Q3	Little Greene No. 105	11,92	Окраска, Farrow & Ball Modern Emulsion, матовая, 2 слоя, подготовка Q3 Акцент — стена А: окраска, Farrow & Ball Modern Emulsion, матовая, 2 слоя, подготовка Q3	Farrow & Ball No. 226 Farrow & Ball No. 298	25,30 5,68	Плинтус МДФ h=80 мм, аналог: МДФ под покраску 80×16	Farrow & Ball No. 226	11,7	Инженерная доска, 1167-4250, 2100×127 мм, на клею; тип 2, отм. ЧП ±0,000	11,92	Н стен 2700 (до потолка); краска бренда веера Little Greene; класс по EN 13300 и блеск линейки — по ТУ Little Greene, в базе не сверены; плинтус в цвет: стены
3	Санузел 1 этажа 4,87 м²	ГКЛВ по каркасу П113, отм. +2,600; окраска, Little Greene Intelligent Bathroom, матовая, 2 слоя, подготовка Q3	Little Greene No. 105	4,87	Облицовка плиткой, A8UZ, 600×1200×9 мм, клей C2 TE S1, затирка CG2WA	Atlas Concorde A8UZ	20,53	нет			Аналог: керамогранит ректифицированный под травертин, матовый, 600×600×9 мм; тип 3, отм. ЧП −0,015	4,87	Н стен 2615 (до потолка); гидроизоляция обмазочная, 2 слоя, по всему помещению, с заведением на стены 200 мм; у душа — на всю высоту стен душевой зоны и 500 мм за край душевой зоны (по пирогу пола); тест проливом и акт скрытых работ; краска бренда веера Little Greene класс по EN 13300 и блеск линейки — по ТУ Little Greene, в базе не сверены
4	Котельная 6,88 м²	Потолок под покраску, отм. +2,800; окраска, Little Greene Absolute Matt, глубокоматовая, 2 слоя, подготовка Q3	Little Greene No. 105	6,88	Окраска, Farrow & Ball Modern Emulsion, матовая, 2 слоя, подготовка Q3	Farrow & Ball No. 226	26,96	Плинтус МДФ h=80 мм, аналог: МДФ под покраску 80×16	Farrow & Ball No. 226	9,7	Керамогранит, A8UZ, 600×1200×9 мм; тип 4, отм. ЧП ±0,000	6,88	Н стен 2800 (до потолка); матовая моющаяся, класс 1 EN 13300 — осознанно вместо полуматовой; краска бренда веера Little Greene класс по EN 13300 и блеск линейки — по ТУ Little Greene, в базе не сверены; плинтус в цвет: стены
5	Гостиная 33,74 м²	ГКЛ по каркасу П113, отм. +2,600; +2,700; окраска, Tikkurila Anti-Reflex 2, глубокоматовая, 2 слоя, подготовка Q3	NCS S 0804-Y30R	33,74	Окраска, Tikkurila Optiva 5 Matt, матовая, 2 слоя, подготовка К3 Акцент — стена А: окраска, Farrow & Ball Modern Emulsion, матовая, 3 слоя, аналог: интерьерная краска, класс 2 по EN 13300, глубокоматовая/матовая, база С, подготовка К3	NCS S 0804-Y30R Farrow & Ball No. 93	32,20 12,92	Плинтус МДФ h=80 мм, аналог: МДФ под окраску 80×16 мм	NCS S 0804-Y30R	18,2	Инженерная доска, 1167-4250, 2100×127 мм, на клею; тип 5, отм. ЧП ±0,000	33,74	Н стен 2600 (до потолка); колеруется в код стен, но по эмали на МДФ: сличать отдельным выкрасом на своей подложке (выкрас № 10); плинтус в цвет: стены

Примечания

1. Ведомость продолжена на листе 2 из 4; итоги, сводка площадей и примечания — на последнем листе ведомости.

Допущения и предложения на листе

Основа листа: размеры и контуры этажей подобраны проектировщиком по составу помещений и площадям этажей с картинки 470 px (размеры на ней не читаются); обмер и исходный проект — задание (К-1); высоты: 1-й этаж 2800 мм, мансарда 2700 мм (горизонтальная часть) приняты; скаты кровли мансарды приняты по картинке: колено 1200 мм, уклон 45°, конёк вдоль длинной стороны; проект КР — задание (К-2); наружные стены 400 мм, перегородки 120 мм приняты (К-1); разрешённая мощность 15 кВт принята по типовым ТУ для частного дома (К-4); подрайон климата не задан — принят не северный (жилые от 2,5 м) (К-7).

Знак «*» — принято, не замерено и не подтверждено (замерить на объекте): К-13: пол пом. 11, 12 — отметка верха плиты −0,170 принята по пирогу (плита веранды и крыльца своя, ниже плиты дома) — подтвердить по проекту КР или обмером (К-13).

Знак «**» — предложение проектировщика, заказчиком не утверждено (согласовать с заказчиком): плинтус пом. 1, 2, 4–14, 16, 17, фартук пом. 1, акцент пом. 5 — артикул изделия не выбран: позиция описана характеристиками («аналог по характеристикам»), артикул выбирается при закупке; пол пом. 3, 15, 20 — пирог пола: стяжка 33 мм и обмазочная гидроизоляция добавлены разработчиком проекта; артикул изделия не выбран: позиция описана характеристиками («аналог по характеристикам»), артикул выбирается при закупке; пол пом. 10 — покрытие пола гаража — предложение исполнителя: выдерживает шины, масло и антигололёдные реагенты, без швов.

См. лист открытых вопросов (лист 8, записи К-1, К-2, К-4, К-7; лист 9, запись К-13).

Изм.	Кол.уч	Лист	№ док.	Подп.	Дата
Разраб.		Кырлан А.С.			04.11.26
Пров.					
ГИП					
Н. контр.					
Утв.					

ГД-2026-010-АИ

Дом 331 м²

Общая площадь 270,67* м² · * размеры приняты, не замерены (реестр — л. 8–10, К-1)

Дизайн-проект интерьера	Стадия	Лист	Листов
	РП	91	216
Ведомость отделки помещений. Лист 1 из 4 М б/м	**Кырлан Александр Сергеевич**		

выпуск 04.11.2026 № 2a77323a49 · стр. 93 из 221

Ведомость отделки помещений. Лист 2 из 4

Потолки, стены, низ стен, полы · площади в м², длины в м · отметки в м

Ведомость отделки помещений (форма 1 прил. А ГОСТ 21.501-2018). Лист 2 из 4

№	Наименование помещения	Потолок			Стены и перегородки			Низ стен (плинтус)			Пол		Примечание
		Вид отделки	Код цвета	S, м²	Вид отделки	Код цвета	S, м²	Вид отделки	Код цвета	L, м	Вид отделки	S, м²	
6	Холл с лестницей 10,02 м²	ГКЛ по каркасу П113, отм. +2,700; окраска, Little Greene Absolute Matt, глубокоматовая, 2 слоя, подготовка Q3	Little Greene No. 105	10,02	Окраска, Farrow & Ball Modern Emulsion, матовая, 2 слоя, подготовка Q3	Farrow & Ball No. 226	22,29	Плинтус МДФ h=80 мм, аналог: МДФ под покраску 80×16	Farrow & Ball No. 226	7,0	Инженерная доска, 1167-4250, 2100×127 мм, на клею; тип 2, отм. ЧП ±0,000	10,02	Н стен 2700 (до потолка); матовая моющаяся, класс 1 EN 13300 — осознанно вместо полуматовой; краска бренда веера Little Greene класс по EN 13300 и блеск линейки — по ТУ Little Greene, в базе не сверены; плинтус в цвет: стены
7	Кладовая 5,99 м²	Потолок под покраску, отм. +2,800; окраска, Little Greene Absolute Matt, глубокоматовая, 2 слоя, подготовка Q3	Little Greene No. 105	5,99	Окраска, Little Greene Intelligent Matt, матовая, 2 слоя, подготовка Q3	Little Greene No. 105	23,28	Плинтус МДФ h=80 мм, аналог: МДФ под покраску 80×16	Little Greene No. 105	7,8	Инженерная доска, 1167-4250, 2100×127 мм, на клею; тип 2, отм. ЧП ±0,000	5,99	Н стен 2800 (до потолка); краска бренда веера Little Greene; класс по EN 13300 и блеск линейки — по ТУ Little Greene, в базе не сверены; краска бренда веера Little Greene класс по EN 13300 и блеск линейки — по ТУ Little Greene, в базе не сверены; плинтус в цвет: стены
8	Прихожая 12,46 м²	ГКЛ по каркасу П113, отм. +2,700; окраска, Little Greene Absolute Matt, глубокоматовая, 2 слоя, подготовка Q3	Little Greene No. 105	12,46	Окраска, Farrow & Ball Modern Emulsion, матовая, 2 слоя, подготовка Q3	Farrow & Ball No. 226	38,99	Плинтус МДФ h=80 мм, аналог: МДФ под покраску 80×16	Farrow & Ball No. 226	13,6	Керамогранит, A8UZ, 600×1200×9 мм; тип 4, отм. ЧП ±0,000	12,46	Н стен 2700 (до потолка); матовая моющаяся, класс 1 EN 13300 — осознанно вместо полуматовой; краска бренда веера Little Greene класс по EN 13300 и блеск линейки — по ТУ Little Greene, в базе не сверены; плинтус в цвет: стены
9	Тамбур 3,49 м²	Потолок под покраску, отм. +2,800; окраска, Little Greene Absolute Matt, глубокоматовая, 2 слоя, подготовка Q3	Little Greene No. 105	3,49	Окраска, Farrow & Ball Modern Emulsion, матовая, 2 слоя, подготовка Q3	Farrow & Ball No. 226	17,07	Плинтус МДФ h=80 мм, аналог: МДФ под покраску 80×16	Farrow & Ball No. 226	5,6	Керамогранит, A8UZ, 600×1200×9 мм; тип 4, отм. ЧП ±0,000	3,49	Н стен 2800 (до потолка); матовая моющаяся, класс 1 EN 13300 — осознанно вместо полуматовой; краска бренда веера Little Greene класс по EN 13300 и блеск линейки — по ТУ Little Greene, в базе не сверены; плинтус в цвет: стены
10	Гараж 41,58 м²	Потолок под покраску, отм. +2,800; окраска, Little Greene Absolute Matt, глубокоматовая, 2 слоя, подготовка Q3	Little Greene No. 105	41,58	Окраска, Farrow & Ball Modern Emulsion, матовая, 2 слоя, подготовка Q3	Farrow & Ball No. 226	62,59	Плинтус ПВХ h=100 мм, аналог: ПВХ влагостойкий 100 мм, серый		22,0	Аналог: наливной полимерный пол (эпоксидный), с кварцевой посыпкой, 3 мм; тип 6, отм. ЧП ±0,000	41,58	Н стен 2800 (до потолка); матовая моющаяся, класс 1 EN 13300 — осознанно вместо полуматовой; краска бренда веера Little Greene класс по EN 13300 и блеск линейки — по ТУ Little Greene, в базе не сверены

Примечания

1. Ведомость продолжена на листе 3 из 4; итоги, сводка площадей и примечания — на последнем листе ведомости.

Допущения и предложения на листе

Основа листа: размеры и контуры этажей подобраны проектировщиком по составу помещений и площадям этажей с картинки 470 px (размеры на ней не читаются); обмер и исходный проект — задание (К-1); высоты: 1-й этаж 2800 мм, мансарда 2700 мм (горизонтальная часть) приняты; скаты кровли мансарды приняты по картинке: колено 1200 мм, уклон 45°, конёк вдоль длинной стороны; проект КР — задание (К-2); наружные стены 400 мм, перегородки 120 мм приняты (К-1); разрешённая мощность 15 кВт принята по типовым ТУ для частного дома (К-4); подрайон климата не задан — принят не северный (жилые от 2,5 м) (К-7).

Знак «*» — принято, не замерено и не подтверждено (замерить на объекте): К-13: пол пом. 11, 12 — отметка верха плиты −0,170 принята по пирогу (плита веранды и крыльца своя, ниже плиты дома) — подтвердить по проекту КР или обмером (К-13).

Знак «**» — предложение проектировщика, заказчиком не утверждено (согласовать с заказчиком): плинтус пом. 1, 2, 4–14, 16, 17, фартук пом. 1, акцент пом. 5 — артикул изделия не выбран: позиция описана характеристиками («аналог по характеристикам»), артикул выбирается при закупке; пол пом. 3, 15, 20 — пирог пола: стяжка 33 мм и обмазочная гидроизоляция добавлены разработчиком проекта; артикул изделия не выбран: позиция описана характеристиками («аналог по характеристикам»), артикул выбирается при закупке; пол пом. 10 — покрытие пола гаража — предложение исполнителя: выдерживает шины, масло и антигололёдные реагенты, без швов.

См. лист открытых вопросов (лист 8, записи К-1, К-2, К-4, К-7; лист 9, запись К-13).

Изм.	Кол.уч	Лист	№ док.	Подп.	Дата
Разраб.		Кырлан А.С.			04.11.26
Пров.					
ГИП					
Н. контр.					
Утв.					

ГД-2026-010-АИ

Дом 331 м²

Общая площадь 270,67* м² · * размеры приняты, не замерены (реестр — л. 8–10, К-1)

Дизайн-проект интерьера	Стадия	Лист	Листов
	РП	92	216

Ведомость отделки помещений. Лист 2 из 4

М б/м

Кырлан Александр Сергеевич

выпуск 04.11.2026 № 2a77323a49 · стр. 94 из 221

Ведомость отделки помещений. Лист 3 из 4

Потолки, стены, низ стен, полы · площади в м², длины в м · отметки в м

Ведомость отделки помещений (форма 1 прил. А ГОСТ 21.501-2018). Лист 3 из 4

№	Наименование помещения	Потолок			Стены и перегородки			Низ стен (плинтус)			Пол		Примечание
		Вид отделки	Код цвета	S, м²	Вид отделки	Код цвета	S, м²	Вид отделки	Код цвета	L, м	Вид отделки	S, м²	
11	Веранда 21,84 м²	Потолок под покраску (летнее помещение), отм. +2,800; окраска, Tikkurila Luja 7, матовая, 2 слоя, подготовка Q3	NCS S 0804-Y30R	21,84	Окраска, Tikkurila Luja 7, полуматовая, 2 слоя, подготовка К3	NCS S 0804-Y30R	49,63	Плинтус из керамогранита h=80 мм, аналог: из керамогранита пола, подрезка 80 мм, верхняя кромка с запилом 45°	#B8AFA5	20,5	Керамогранит, A8UZ, 600×1200×10 мм; тип 7, отм. ЧП −0,030	21,84	Н стен 2830 (до потолка); влагостойкая окраска по утеплённой стене; категория К3 по СП 71.13330.2017, табл. 7.5; по ГКЛВ каркаса П113, влагостойкая окраска; Q3
12	Крыльцо 3,38 м²	Потолок под покраску (летнее помещение), отм. +2,800; окраска, Tikkurila Luja 7, матовая, 2 слоя, подготовка Q3	NCS S 0804-Y30R	3,38	Окраска, Tikkurila Luja 7, полуматовая, 2 слоя, подготовка К3	NCS S 0804-Y30R	18,73	Плинтус из керамогранита h=80 мм, аналог: из керамогранита пола, подрезка 80 мм, верхняя кромка с запилом 45°	#B8AFA5	6,4	Керамогранит, A8UZ, 600×1200×10 мм; тип 7, отм. ЧП −0,030	3,38	Н стен 2830 (до потолка); влагостойкая окраска по утеплённой стене; категория К3 по СП 71.13330.2017, табл. 7.5; по ГКЛВ каркаса П113, влагостойкая окраска; Q3
13	Спальня мастер 24,59 м²	ГКЛ по каркасу П113, отм. +5,650; +5,750; окраска, Little Greene Absolute Matt, глубокоматовая, 2 слоя, подготовка Q3	Little Greene No. 105	27,05	Окраска, Farrow & Ball Modern Emulsion, матовая, 2 слоя, подготовка Q3 Акцент — стена А: окраска, Tikkurila Optiva 5 Matt, матовая, 2 слоя, подготовка Q3	Farrow & Ball No. 226 NCS S 7020-G10Y	28,61 7,60	Плинтус МДФ h=80 мм, аналог: МДФ под покраску 80×16	Farrow & Ball No. 226	18,7	Инженерная доска, 1167-4250, 2100×127 мм, на клею; тип 2, отм. ЧП +3,150	24,59	Н стен 2500 (до потолка); краска бренда веера Little Greene; класс по EN 13300 и блеск линейки — по ТУ Little Greene, в базе не сверены; плинтус в цвет: стены
14	Гардеробная мастер 6,74 м²	Обшивка скатов и горизонтальной части мансарды (конструкция — по проекту КР), отм. +5,850; окраска, Little Greene Absolute Matt, глубокоматовая, 2 слоя, подготовка Q3	Little Greene No. 105	8,56	Окраска, Little Greene Intelligent Matt, матовая, 2 слоя, подготовка Q3	Little Greene No. 105	18,68	Плинтус МДФ h=80 мм, аналог: МДФ под покраску 80×16	Little Greene No. 105	9,0	Инженерная доска, 1167-4250, 2100×127 мм, на клею; тип 2, отм. ЧП +3,150	6,74	Н стен 2700 (до потолка); краска бренда веера Little Greene; класс по EN 13300 и блеск линейки — по ТУ Little Greene, в базе не сверены; краска бренда веера Little Greene класс по EN 13300 и блеск линейки — по ТУ Little Greene, в базе не сверены; плинтус в цвет: стены
15	Санузел мастер 6,88 м²	ГКЛВ по каркасу П113, отм. +5,750; окраска, Little Greene Intelligent Bathroom, матовая, 2 слоя, подготовка Q3	Little Greene No. 105	7,84	Облицовка плиткой, A8UZ, 600×1200×9 мм, клей C2 TE S1, затирка CG2WA	Atlas Concorde A8UZ	19,94	нет			Аналог: керамогранит ректифицированный под травертин, матовый, 600×600×9 мм; тип 3, отм. ЧП +3,135	6,88	Н стен 2615 (до потолка); гидроизоляция обмазочная, 2 слоя, с заведением на стены 200 мм; над ванной — до 2000 и 300 мм за борт (по пирогу пола); тест проливом и акт скрытых работ; краска бренда веера Little Greene класс по EN 13300 и блеск линейки — по ТУ Little Greene, в базе не сверены
16	Спальня 2 15,52 м²	ГКЛ по каркасу П113, отм. +5,750; +5,650; окраска, Little Greene Absolute Matt, глубокоматовая, 2 слоя, подготовка Q3	Little Greene No. 105	15,52	Окраска, Farrow & Ball Modern Emulsion, матовая, 2 слоя, подготовка Q3 Акцент — стена А: окраска, Farrow & Ball Modern Emulsion, матовая, 2 слоя, подготовка Q3	Farrow & Ball No. 226 Farrow & Ball No. 64	28,08 7,35	Плинтус МДФ h=80 мм, аналог: МДФ под покраску 80×16	Farrow & Ball No. 226	14,7	Инженерная доска, 1167-4250, 2100×127 мм, на клею; тип 2, отм. ЧП +3,150	15,52	Н стен 2500 (до потолка); краска бренда веера Little Greene; класс по EN 13300 и блеск линейки — по ТУ Little Greene, в базе не сверены; плинтус в цвет: стены

Примечания

1. Ведомость продолжена на листе 4 из 4; итоги, сводка площадей и примечания — на последнем листе ведомости.

Допущения и предложения на листе. Основа листа: размеры и контуры этажей подобраны проектировщиком по составу помещений и площадям этажей с картинки 470 px (размеры на ней не читаются); обмер и исходный проект — задание (К-1); высоты: 1-й этаж 2800 мм, мансарда 2700 мм (горизонтальная часть) приняты; скаты кровли мансарды приняты по картинке: колено 1200 мм, уклон 45°, конёк вдоль длинной стороны; проект КР — задание (К-2); наружные стены 400 мм, перегородки 120 мм приняты (К-1); разрешённая мощность 15 кВт принята по типовым ТУ для частного дома (К-4); подрайон климата не задан — принят не северный (жилые от 2,5 м) (К-7). Знак «*» — принято, не замерено и не подтверждено (замерить на объекте): К-13: пол пом. 11, 12 — отметка верха плиты −0,170 принята по пирогу (плита веранды и крыльца своя, ниже плиты дома) — подтвердить по проекту КР или обмером (К-13). Знак «**» — предложение проектировщика, заказчиком не утверждено (согласовать с заказчиком): плинтус пом. 1, 2, 4–14, 16, 17, фартук пом. 1, акцент пом. 5 — артикул изделия не выбран: позиция описана характеристиками («аналог по характеристикам»), артикул выбирается при закупке; пол пом. 3, 15, 20 — пирог пола: стяжка 33 мм и обмазочная гидроизоляция добавлены разработчиком проекта; артикул изделия не выбран: позиция описана характеристиками («аналог по характеристикам»), артикул выбирается при закупке; пол пом. 10 — покрытие пола гаража — предложение исполнителя: выдерживает шины, масло и антигололёдные реагенты, без швов. См. лист открытых вопросов (лист 8, записи К-1, К-2, К-4, К-7; лист 9, запись К-13).

Изм.	Кол.уч	Лист	№ док.	Подп.	Дата
Разраб.		Кырлан А.С.			04.11.26
Пров.					
ГИП					
Н. контр.					
Утв.					

ГД-2026-010-АИ

Дом 331 м²

Общая площадь 270,67* м² · * размеры приняты, не замерены (реестр — л. 8–10, К-1)

Дизайн-проект интерьера

Стадия	Лист	Листов
РП	93	216

Ведомость отделки помещений. Лист 3 из 4

М б/м

Кырлан Александр Сергеевич

выпуск 04.11.2026 № 2a77323a49 · стр. 95 из 221

Ведомость отделки помещений. Лист 4 из 4

Потолки, стены, низ стен, полы · площади в м², длины в м · отметки в м

Ведомость отделки помещений (форма 1 прил. А ГОСТ 21.501-2018). Лист 4 из 4

№	Наименование помещения	Потолок			Стены и перегородки			Низ стен (плинтус)			Пол		Примечание
		Вид отделки	Код цвета	S, м²	Вид отделки	Код цвета	S, м²	Вид отделки	Код цвета	L, м	Вид отделки	S, м²	
17	Холл мансарды 21,72 м²	ГКЛ по каркасу П113, отм. +5,750; окраска, Little Greene Absolute Matt, глубокоматовая, 2 слоя, подготовка Q3	Little Greene No. 105	23,52	Окраска, Farrow & Ball Modern Emulsion, матовая, 2 слоя, подготовка Q3	Farrow & Ball No. 226	34,75	Плинтус МДФ h=80 мм, аналог: МДФ под покраску 80×16	Farrow & Ball No. 226	14,4	Инженерная доска, 1167-4250, 2100×127 мм, на клею; тип 2, отм. ЧП +3,150	21,72	Н стен 2600 (до потолка); матовая моющаяся, класс 1 EN 13300 — осознанно вместо полуматовой; краска бренда веера Little Greene класс по EN 13300 и блеск линейки — по ТУ Little Greene, в базе не сверены; плинтус в цвет: стены
18	Спальня 3 17,11 м²	ГКЛ по каркасу П113, отм. +5,650; +5,750; окраска, Little Greene Absolute Matt, глубокоматовая, 2 слоя, подготовка Q3	Little Greene No. 105	17,11	Окраска, Farrow & Ball Modern Emulsion, матовая, 2 слоя, подготовка Q3 Акцент — стена А: окраска, Tikkurila Optiva 5 Matt, матовая, 2 слоя, подготовка Q3	Farrow & Ball No. 226 NCS S 3020-G30Y	25,47 12,33	Плинтус МДФ h=69 мм, SX165	Farrow & Ball No. 226	15,6	Инженерная доска, 1167-4250, 2100×127 мм, на клею; тип 2, отм. ЧП +3,150	17,11	Н стен 2500 (до потолка); краска бренда веера Little Greene; класс по EN 13300 и блеск линейки — по ТУ Little Greene, в базе не сверены; плинтус в цвет: стены
19	Спальня 4 16,28 м²	ГКЛ по каркасу П113, отм. +5,650; +5,750; окраска, Little Greene Absolute Matt, глубокоматовая, 2 слоя, подготовка Q3	Little Greene No. 105	18,76	Окраска, Farrow & Ball Modern Emulsion, матовая, 2 слоя, подготовка Q3 Акцент — стена А: окраска, Tikkurila Optiva 5 Matt, матовая, 2 слоя, подготовка Q3	Farrow & Ball No. 226 NCS S 3040-Y70R	15,83 14,85	Плинтус МДФ h=69 мм, SX165	Farrow & Ball No. 226	16,6	Инженерная доска, 1167-4250, 2100×127 мм, на клею; тип 2, отм. ЧП +3,150	16,28	Н стен 2500 (до потолка); краска бренда веера Little Greene; класс по EN 13300 и блеск линейки — по ТУ Little Greene, в базе не сверены; плинтус в цвет: стены
20	Санузел 2 6,29 м²	ГКЛВ по каркасу П113, отм. +5,750; окраска, Little Greene Intelligent Bathroom, матовая, 2 слоя, подготовка Q3	Little Greene No. 105	8,15	Облицовка плиткой, A8UZ, 600×1200×9 мм, клей C2 TE S1, затирка CG2WA	Atlas Concorde A8UZ	17,76	нет			Аналог: керамогранит ректифицированный под травертин, матовый, 600×600×9 мм; тип 3, отм. ЧП +3,135	6,29	Н стен 2615 (до потолка); гидроизоляция обмазочная, 2 слоя, с заведением на стены 200 мм; у душа — до 2000 и 500 мм за поддон (по пирогу пола); тест проливом и акт скрытых работ; краска бренда веера Little Greene класс по EN 13300 и блеск линейки — по ТУ Little Greene, в базе не сверены
	Итого			**307,27**			**633,37**			**229,8**		**295,89**	

Допущения и предложения на листе. Основа листа: размеры и контуры этажей подобраны проектировщиком по составу помещений и площадям этажей с картинки 470 px (размеры на ней не читаются); обмер и исходный проект — задание (К-1); высоты: 1-й этаж 2800 мм, мансарда 2700 мм (горизонтальная часть) приняты; скаты кровли мансарды приняты по картинке: колено 1200 мм, уклон 45°, конёк вдоль длинной стороны; проект КР — задание (К-2); наружные стены 400 мм, перегородки 120 мм приняты (К-1); разрешённая мощность 15 кВт принята по типовым ТУ для частного дома (К-4); подрайон климата не задан — принят не северный (жилые от 2,5 м) (К-7). Знак «*» — принято, не замерено и не подтверждено (замерить на объекте): К-13: пол пом. 11, 12 — отметка верха плиты −0,170 принята по пирогу (плита веранды и крыльца своя, ниже плиты дома) — подтвердить по проекту КР или обмером (К-13). Знак «**» — предложение проектировщика, заказчиком не утверждено (согласовать с заказчиком): плинтус пом. 1, 2, 4–14, 16, 17, фартук пом. 1, акцент пом. 5 — артикул изделия не выбран: позиция описана характеристиками («аналог по характеристикам»), артикул выбирается при закупке; пол пом. 3, 15, 20 — пирог пола: стяжка 33 мм и обмазочная гидроизоляция добавлены разработчиком проекта; артикул изделия не выбран: позиция описана характеристиками («аналог по характеристикам»), артикул выбирается при закупке; пол пом. 10 — покрытие пола гаража — предложение исполнителя: выдерживает шины, масло и антигололёдные реагенты, без швов. См. лист открытых вопросов (лист 8, записи К-1, К-2, К-4, К-7; лист 9, запись К-13).

Примечания

1. Площади поверхностей — по чистым граням стен до отделки: стены = периметр × высоту от чистого пола помещения до низа потолка минус проёмы (облицовка плиткой — до верха облицовки); плинтус = периметр минус дверные проёмы; пол и потолок — по площади помещения. Количество плиток по раскладке. Площади помещений — с учётом всех частей помещения; откосы в площадь стен не входят.
2. Акцентные стены и фартук — отдельными строками, их площадь вычтена из основной отделки стен помещения; фартук — над нижними модулями кухни от столешницы до низа навесных шкафов, где шкафов нет — на 600 мм.
3. Плинтус — длина по периметру за вычетом дверных проёмов; примыкания к наличникам и встроенной мебели — по развёрткам.
4. Формат плитки — Ш×В×Т (ширина × высота в положении укладки × толщина), мм; на полу — вдоль стен А/В × вдоль стен Б/Г.
5. Коды цвета — по веерам производителей; колеровка каждой краски одной партией, проверка выкраса при свете D65 и при лампах проекта.
6. Уровни подготовки Q1–Q4 — система Knauf, не норма ГОСТ/СП; допуски поверхностей — по СП 71.13330.2017 (действующая редакция).
7. «аналог:» — изделие задано характеристиками, марку и артикул согласовать с заказчиком до закупки.
8. Плавающая стяжка по звукоизоляции: демпферная (кромочная) лента по контуру помещения и у стояков (СП 51.13330.2011, п. 9.11); плинтус крепится только к стене.
9. Сводка площадей по материалам, м²: потолок — NCS S 0804-Y30R Luja 7 — 49,81; потолок — Little Greene No. 105 Absolute Matt — 202,86; потолок — Little Greene No. 105 Intelligent Bathroom — 20,86; потолок — NCS S 0804-Y30R Anti-Reflex 2 — 33,74; стены — NCS S 0804-Y30R Luja 7 — 113,16; стены — Farrow & Ball No. 226 Modern Emulsion — 325,94; стены — Farrow & Ball No. 298 Modern Emulsion — 5,68; стены — облицовка плиткой 600×1200×9 мм, Atlas Concorde A8UZ — 58,23; стены — NCS S 0804-Y30R Optiva 5 Matt — 32,20; стены — Farrow & Ball No. 93 Modern Emulsion — 12,92; стены — Little Greene No. 105 Intelligent Matt — 41,96; стены — NCS S 7020-G10Y Optiva 5 Matt — 7,60; стены — Farrow & Ball No. 64 Modern Emulsion — 7,35; стены — NCS S 3020-G30Y Optiva 5 Matt — 12,33; стены — NCS S 3040-Y70R Optiva 5 Matt — 14,85; фартук облицовка керамогранитом, #F1F1EC — 1,15.

Изм.	Кол.уч	Лист	№ док.	Подп.	Дата
Разраб.		Кырлан А.С.			04.11.26
Пров.					
ГИП					
Н. контр.					
Утв.					

ГД-2026-010-АИ

Дом 331 м²

Общая площадь 270,67* м² · * размеры приняты, не замерены (реестр — л. 8–10, К-1)

Дизайн-проект интерьера

Стадия	Лист	Листов
РП	94	216

Ведомость отделки помещений. Лист 4 из 4

М б/м

Кырлан Александр Сергеевич

Колерная карта

Цвета и материалы по помещениям · палитра проекта · лист 1 из 2

Колерная карта по помещениям

Помещение	Поверхность	Образец	Поз.	Система и код цвета	Производитель, линейка / материал, артикул	Блеск	Класс истирания	LRV	Площадь
1. Кухня-столовая 24,59 м²	стены		**К1**	NCS S 0804-Y30R	Tikkurila · Luja 7	полуматов.	1	85	44,8 м²
	потолок		**К2**	NCS S 0804-Y30R	Tikkurila · Luja 7	матовая	1	85	24,6 м²
	пол		**КМ1**	по образцу	Coswick · Вековые традиции · арт. 1167-4250				24,6 м²
	плинтус		**К3**	NCS S 0804-Y30R	МДФ · в цвет NCS	полуглянц.	2	85	18,3 м
	фартук		**КМ2**	тон Paper F497 (тёплый белый)	керамогранит · аналог по хар.				1,1 м²
2. Кабинет-гостевая 11,92 м²	стены		**К4**	Farrow & Ball No. 226	Farrow & Ball · Modern Emulsion	матовая	1	63	25,3 м²
	акцент А		**К5**	Farrow & Ball No. 298	Farrow & Ball · Modern Emulsion	матовая	1	14	5,7 м²
	потолок		**К6**	Little Greene No. 105	Little Greene · Absolute Matt	глубокомат.	2	82	11,9 м²
	пол		**КМ1**	по образцу	Coswick · Вековые традиции · арт. 1167-4250				11,9 м²
	плинтус		**К7**	Farrow & Ball No. 226	МДФ · в цвет Farrow & Ball			63	11,7 м
3. Санузел 1 этажа 4,87 м²	стены		**КМ3**	Marvel Travertine	Atlas Concorde · арт. A8UZ				20,5 м²
	потолок		**К8**	Little Greene No. 105	Little Greene · Intelligent Bathroom	матовая	1	82	4,9 м²
	пол		**КМ4**	по образцу	керамогранит · аналог по хар.				4,9 м²
4. Котельная 6,88 м²	стены		**К4**	Farrow & Ball No. 226	Farrow & Ball · Modern Emulsion	матовая	1	63	27,0 м²
	потолок		**К6**	Little Greene No. 105	Little Greene · Absolute Matt	глубокомат.	2	82	6,9 м²
	пол		**КМ5**	Marvel Travertine	Atlas Concorde · арт. A8UZ				6,9 м²
	плинтус		**К7**	Farrow & Ball No. 226	МДФ · в цвет Farrow & Ball			63	9,7 м
5. Гостиная 33,74 м²	стены		**К9**	NCS S 0804-Y30R	Tikkurila · Optiva 5 Matt	матовая	2	85	32,2 м²
	акцент А		**К10**	Farrow & Ball No. 93	Farrow & Ball · Modern Emulsion	матовая	1	7	12,9 м²
	потолок		**К11**	NCS S 0804-Y30R	Tikkurila · Anti-Reflex 2	глубокомат.	2	85	33,7 м²
	пол		**КМ1**	по образцу	Coswick · Вековые традиции · арт. 1167-4250				33,7 м²
	плинтус		**К3**	NCS S 0804-Y30R	МДФ · в цвет NCS	полуглянц.	2	85	18,2 м
6. Холл с лестницей 10,02 м²	стены		**К4**	Farrow & Ball No. 226	Farrow & Ball · Modern Emulsion	матовая	1	63	22,3 м²
	потолок		**К6**	Little Greene No. 105	Little Greene · Absolute Matt	глубокомат.	2	82	10,0 м²
	пол		**КМ1**	по образцу	Coswick · Вековые традиции · арт. 1167-4250				10,0 м²
	плинтус		**К7**	Farrow & Ball No. 226	МДФ · в цвет Farrow & Ball			63	7,0 м
7. Кладовая 5,99 м²	стены		**К12**	Little Greene No. 105	Little Greene · Intelligent Matt	матовая	1	82	23,3 м²
	потолок		**К6**	Little Greene No. 105	Little Greene · Absolute Matt	глубокомат.	2	82	6,0 м²
	пол		**КМ1**	по образцу	Coswick · Вековые традиции · арт. 1167-4250				6,0 м²
	плинтус		**К13**	Little Greene No. 105	МДФ · в цвет Little Greene			82	7,8 м
8. Прихожая 12,46 м²	стены		**К4**	Farrow & Ball No. 226	Farrow & Ball · Modern Emulsion	матовая	1	63	39,0 м²
	потолок		**К6**	Little Greene No. 105	Little Greene · Absolute Matt	глубокомат.	2	82	12,5 м²
	пол		**КМ5**	Marvel Travertine	Atlas Concorde · арт. A8UZ				12,5 м²
	плинтус		**К7**	Farrow & Ball No. 226	МДФ · в цвет Farrow & Ball			63	13,6 м
9. Тамбур 3,49 м²	стены		**К4**	Farrow & Ball No. 226	Farrow & Ball · Modern Emulsion	матовая	1	63	17,1 м²
	потолок		**К6**	Little Greene No. 105	Little Greene · Absolute Matt	глубокомат.	2	82	3,5 м²
	пол		**КМ5**	Marvel Travertine	Atlas Concorde · арт. A8UZ				3,5 м²
	плинтус		**К7**	Farrow & Ball No. 226	МДФ · в цвет Farrow & Ball			63	5,6 м
10. Гараж 41,58 м²	стены		**К4**	Farrow & Ball No. 226	Farrow & Ball · Modern Emulsion	матовая	1	63	62,6 м²
	потолок		**К6**	Little Greene No. 105	Little Greene · Absolute Matt	глубокомат.	2	82	41,6 м²
	пол		**КМ6**	по образцу	аналог по хар.				41,6 м²
	плинтус		**КМ7**	по образцу	ПВХ · аналог по хар.				22,0 м

Схема палитры проекта


Стиль: Шале 60% + Эко и органический модерн 40% · схема: комплементарная

основной	основной	основной	второстепенный	второстепенный	второстепенный	второстепенный	второстепенный	второстепенный	второстепенный	второстепенный	акцентный	акцентный	акцентный
Farrow & Ball No. 226	NCS S 0804-Y30R	Little Greene No. 105	Tikkurila V451	NCS S 3020-G30Y	Tikkurila X463	Farrow & Ball No. 229	Farrow & Ball No. 48	Farrow & Ball No. 245	NCS S 2005-Y20R	NCS S 3010-Y30R	NCS S 7020-G10Y	Farrow & Ball No. 64	Farrow & Ball No. 43
Joa's White LRV 63 стены 2,4,6,8,9,10,13,16,17,18,19; плинтус 1,4,6,8,9,10,11,12,15; фартук 2,9	тёплый молочный белый LRV 85 стены 1,5,11,12; потолок 1,5,11; плинтус 5,8	Slaked Lime LRV 82 потолок 2,3,4,5,7,8,9,11,12,13,15,16,17,18,19,20; стены 7,14; плинтус 7,14; фартук 20	Olive grove V451 LRV 51 текстиль/декор 18	шалфей LRV 38 акцент 18; текстиль/декор 17,18	Sandstone X463 LRV 51 текстиль/декор 2,16,19	Elephant's Ear LRV 52 текстиль/декор 13	Mouse's Ear LRV 26 текстиль/декор 2	Charleston Grey LRV 30 текстиль/декор 5,10	Светлый песочно-серый LRV 60 текстиль/декор 1,5,13,18,19	орех/лён тёмный LRV 43 текстиль/декор 2,16,19	Хвойный тёмно-зелёный LRV ≈5 акцент 13; текстиль/декор 13	Red Earth LRV 18 акцент 16; текстиль/декор 16	Eating Room Red LRV 11.8 в отделке не применён

План 60/30/10



Окраска, факт — по площади стен, акцентов, потолков

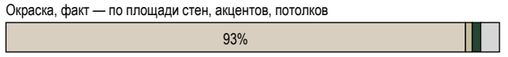

окрашено всего 881,3 м²; серым — цвета вне палитры; второстепенный тон несут мебель и текстиль

Условные обозначения

- **К1** — NCS S 0804-Y30R · тёплый молочный белый · Tikkurila Luja 7 · полуматов. · кл. 1
- **К2** — NCS S 0804-Y30R · тёплый молочный белый · Tikkurila Luja 7 · матовая · кл. 1
- **К3** — NCS S 0804-Y30R · тёплый молочный белый · МДФ · полуглянц. · кл. 2
- **К4** — Farrow & Ball No. 226 · Joa's White · Modern Emulsion · матовая · кл. 1
- **К5** — Farrow & Ball No. 298 · Bancha · Modern Emulsion · матовая · кл. 1
- **К6** — Little Greene No. 105 · Slaked Lime · Absolute Matt · глубокомат. · кл. 2
- **К7** — Farrow & Ball No. 226 · Joa's White · МДФ
- **К8** — Little Greene No. 105 · Slaked Lime · Intelligent Bathroom · матовая · кл. 1
- **К9** — NCS S 0804-Y30R · тёплый молочный белый · Tikkurila Optiva 5 Matt · матовая · кл. 2
- **К10** — Farrow & Ball No. 93 · Studio Green — почти чёрный зелёный · Modern Emulsion · матовая · кл. 1
- дерево (доска, паркет, ламинат) — рисунок досок
- керамогранит, плитка, камень — сетка швов по формату
- материал без кода цвета — по образцу (артикул в ведомости отделки)

- **К11** — NCS S 0804-Y30R · тёплый молочный белый · Tikkurila Anti-Reflex 2 · глубокомат. · кл. 2
- **К12** — Little Greene No. 105 · Slaked Lime · Intelligent Matt · матовая · кл. 1
- **К13** — Little Greene No. 105 · Slaked Lime · МДФ
- **КМ1** — инженерная доска · 1167-4250
- **КМ2** — аналог: керамогранит матовый, тон F497, 600×600×9 мм
- **КМ3** — плитка · A8UZ
- **КМ4** — аналог: керамогранит ректифицированный под травертин, матовый, 600×600×9 мм
- **КМ5** — керамогранит · A8UZ
- **КМ6** — аналог: наливной полимерный пол (эпоксидный), с кварцевой посыпкой, 3 мм
- **КМ7** — ПВХ · аналог: плинтус ПВХ влагостойкий 100 мм, серый

К — краска, КМ — отделочный материал (тон КМ — по описанию, эталон — образец материала); кл. — класс истирания (1 — самый стойкий к мытью); LRV — светлота цвета: 0 — чёрный, 100 — белый

Примечания

1. Цвет на листе и на экране — ориентир. До покраски — выкрас на объекте: не меньше А3 (или лист ГКЛ), на грунте под эту краску, не на белой шпаклёвке, в 2 слоя; на обороте — код, бренд, веер, дата. Смотреть днём и вечером, рядом с образцами пола и плитки. Красить только в цвет утверждённого выкраса.
2. Краску заказывать по коду из графы «Система и код цвета» у бренда этого кода, не «аналогом» другого; весь объём одного кода — одной партией, колеруемую краску — за один проход машины.
3. Площади — те же, что в ведомости отделки (лист 91); сколько краски заказать — в спецификации отделочных материалов (лист 97).
4. Колерная карта на 2 листах: обозначения — на каждом (на этом — позиции его помещений), схема и палитра — на первом, выкрасы — на последнем.

Допущения и предложения на листе. Основа листа: размеры и контуры этажей подобраны проектировщиком по составу помещений и площадям этажей с картинки 470 px (размеры на ней не читаются); обмер и исходный проект — задание (К-1); высоты: 1-й этаж 2800 мм, мансарда 2700 мм (горизонтальная часть) приняты; скаты кровли мансарды приняты по картинке: колено 1200 мм, уклон 45°, конёк вдоль длинной стороны; проект КР — задание (К-2); наружные стены 400 мм, перегородки 120 мм приняты (К-1); разрешённая мощность 15 кВт принята по типовым ТУ для частного дома (К-4); подрайон климата не задан — принят не северный (жилые от 2,5 м) (К-7). Знак «*» — принято, не замерено (замерить): К-13: пол пом. 11, 12. Знак «**» — предложено, не утверждено (согласовать): плинтус пом. 1, 2, 4–14, 16, 17, фартук пом. 1, пол пом. 3, 10, 15, 20, акцент пом. 5. См. лист открытых вопросов (лист 8, записи К-1, К-2, К-4, К-7; лист 9, запись К-13).

Изм.	Кол.уч	Лист	№ док.	Подп.	Дата
Разраб.		Кырлан А.С.			04.11.26
Пров.					
ГИП					
Н. контр.					
Утв.					

ГД-2026-010-АИ

Дом 331 м²

Общая площадь 270,67* м² · * размеры приняты, не замерены (реестр — л. 8–10, К-1)

Дизайн-проект интерьера

Стадия	Лист	Листов
РП	95	216

Колерная карта

М б/м

Кырлан Александр Сергеевич

выпуск 04.11.2026 № 2a77323a49 · стр. 97 из 221

Колерная карта

Цвета и материалы по помещениям · выкрасы на согласование · лист 2 из 2

Колерная карта по помещениям (продолжение)

Помещение	Поверхность	Образец	Поз.	Система и код цвета	Производитель, линейка / материал, артикул	Блеск	Класс истирания	LRV	Площадь
11. Веранда 21,84 м²	стены		**К1**	NCS S 0804-Y30R	Tikkurila · Luja 7	полуматов.	1	85	49,6 м²
	потолок		**К2**	NCS S 0804-Y30R	Tikkurila · Luja 7	матовая	1	85	21,8 м²
	пол		**КМ5**	тон Claystone V486 (грейж)	Atlas Concorde · Marvel Travertine · арт. A8UZ				21,8 м²
	плинтус		**КМ8**	тон Claystone V486 (грейж)	керамогранит · аналог по хар.				20,5 м
12. Крыльцо 3,38 м²	стены		**К1**	NCS S 0804-Y30R	Tikkurila · Luja 7	полуматов.	1	85	18,7 м²
	потолок		**К2**	NCS S 0804-Y30R	Tikkurila · Luja 7	матовая	1	85	3,4 м²
	пол		**КМ5**	тон Claystone V486 (грейж)	Atlas Concorde · Marvel Travertine · арт. A8UZ				3,4 м²
	плинтус		**КМ8**	тон Claystone V486 (грейж)	керамогранит · аналог по хар.				6,4 м
13. Спальня мастер 24,59 м²	стены		**К4**	Farrow & Ball No. 226	Farrow & Ball · Modern Emulsion	матовая	1	63	28,6 м²
	акцент А		**К14**	NCS S 7020-G10Y	Tikkurila · Optiva 5 Matt	матовая	2	≈5	7,6 м²
	потолок		**К6**	Little Greene No. 105	Little Greene · Absolute Matt	глубокомат.	2	82	27,1 м²
	пол		**КМ1**	по образцу	Coswick · Вековые традиции · арт. 1167-4250				24,6 м²
	плинтус		**К7**	Farrow & Ball No. 226	МДФ · в цвет Farrow & Ball			63	18,7 м
14. Гардеробная мастер 6,74 м²	стены		**К12**	Little Greene No. 105	Little Greene · Intelligent Matt	матовая	1	82	18,7 м²
	потолок		**К6**	Little Greene No. 105	Little Greene · Absolute Matt	глубокомат.	2	82	8,6 м²
	пол		**КМ1**	по образцу	Coswick · Вековые традиции · арт. 1167-4250				6,7 м²
	плинтус		**К13**	Little Greene No. 105	МДФ · в цвет Little Greene			82	9,0 м
15. Санузел мастер 6,88 м²	стены		**КМ3**	Marvel Travertine	Atlas Concorde · арт. A8UZ				19,9 м²
	потолок		**К8**	Little Greene No. 105	Little Greene · Intelligent Bathroom	матовая	1	82	7,8 м²
	пол		**КМ4**	по образцу	керамогранит · аналог по хар.				6,9 м²
16. Спальня 2 15,52 м²	стены		**К4**	Farrow & Ball No. 226	Farrow & Ball · Modern Emulsion	матовая	1	63	28,1 м²
	акцент А		**К15**	Farrow & Ball No. 64	Farrow & Ball · Modern Emulsion	матовая	1	18	7,3 м²
	потолок		**К6**	Little Greene No. 105	Little Greene · Absolute Matt	глубокомат.	2	82	15,5 м²
	пол		**КМ1**	по образцу	Coswick · Вековые традиции · арт. 1167-4250				15,5 м²
	плинтус		**К7**	Farrow & Ball No. 226	МДФ · в цвет Farrow & Ball			63	14,7 м
17. Холл мансарды 21,72 м²	стены		**К4**	Farrow & Ball No. 226	Farrow & Ball · Modern Emulsion	матовая	1	63	34,8 м²
	потолок		**К6**	Little Greene No. 105	Little Greene · Absolute Matt	глубокомат.	2	82	23,5 м²
	пол		**КМ1**	по образцу	Coswick · Вековые традиции · арт. 1167-4250				21,7 м²
	плинтус		**К7**	Farrow & Ball No. 226	МДФ · в цвет Farrow & Ball			63	14,4 м
18. Спальня 3 17,11 м²	стены		**К4**	Farrow & Ball No. 226	Farrow & Ball · Modern Emulsion	матовая	1	63	25,5 м²
	акцент А		**К16**	NCS S 3020-G30Y	Tikkurila · Optiva 5 Matt	матовая	2	38	12,3 м²
	потолок		**К6**	Little Greene No. 105	Little Greene · Absolute Matt	глубокомат.	2	82	17,1 м²
	пол		**КМ1**	по образцу	Coswick · Вековые традиции · арт. 1167-4250				17,1 м²
	плинтус		**К17**	Farrow & Ball No. 226	Orac Decor · Contour (Luxxus)			63	15,6 м
19. Спальня 4 16,28 м²	стены		**К4**	Farrow & Ball No. 226	Farrow & Ball · Modern Emulsion	матовая	1	63	15,8 м²
	акцент А		**К18**	NCS S 3040-Y70R	Tikkurila · Optiva 5 Matt	матовая	2	24	14,8 м²
	потолок		**К6**	Little Greene No. 105	Little Greene · Absolute Matt	глубокомат.	2	82	18,8 м²
	пол		**КМ1**	по образцу	Coswick · Вековые традиции · арт. 1167-4250				16,3 м²
	плинтус		**К17**	Farrow & Ball No. 226	Orac Decor · Contour (Luxxus)			63	16,6 м
20. Санузел 2 6,29 м²	стены		**КМ3**	Marvel Travertine	Atlas Concorde · арт. A8UZ				17,8 м²
	потолок		**К8**	Little Greene No. 105	Little Greene · Intelligent Bathroom	матовая	1	82	8,2 м²
	пол		**КМ4**	по образцу	керамогранит · аналог по хар.				6,3 м²

Условные обозначения

- **К1** — NCS S 0804-Y30R · тёплый молочный белый · Tikkurila Luja 7 · полуматов. · кл. 1
- **К2** — NCS S 0804-Y30R · тёплый молочный белый · Tikkurila Luja 7 · матовая · кл. 1
- **К3** — NCS S 0804-Y30R · тёплый молочный белый · МДФ · полуглянц. · кл. 2
- **К4** — Farrow & Ball No. 226 · Joa's White · Modern Emulsion · матовая · кл. 1
- **К5** — Farrow & Ball No. 298 · Bancha · Modern Emulsion · матовая · кл. 1
- **К6** — Little Greene No. 105 · Slaked Lime · Absolute Matt · глубокомат. · кл. 2
- **К7** — Farrow & Ball No. 226 · Joa's White · МДФ
- **К8** — Little Greene No. 105 · Slaked Lime · Intelligent Bathroom · матовая · кл. 1
- **К9** — NCS S 0804-Y30R · тёплый молочный белый · Tikkurila Optiva 5 Matt · матовая · кл. 2
- **К10** — Farrow & Ball No. 93 · Studio Green — почти чёрный зелёный · Modern Emulsion · матовая · кл. 1
- **К11** — NCS S 0804-Y30R · тёплый молочный белый · Tikkurila Anti-Reflex 2 · глубокомат. · кл. 2
- **К12** — Little Greene No. 105 · Slaked Lime · Intelligent Matt · матовая · кл. 1
- **К13** — Little Greene No. 105 · Slaked Lime · МДФ
- **К14** — NCS S 7020-G10Y · Хвойный тёмно-зелёный · Tikkurila Optiva 5 Matt · матовая · кл. 2
- **К15** — Farrow & Ball No. 64 · Red Earth · Modern Emulsion · матовая · кл. 1
- **К16** — NCS S 3020-G30Y · шалфей · Tikkurila Optiva 5 Matt · матовая · кл. 2
- **К17** — Farrow & Ball No. 226 · Joa's White · Contour (Luxxus)
- **К18** — NCS S 3040-Y70R · обожжённая глина · Tikkurila Optiva 5 Matt · матовая · кл. 2
- **КМ1** — инженерная доска · 1167-4250
- **КМ2** — аналог: керамогранит матовый, тон F497, 600×600×9 мм
- **КМ3** — плитка · A8UZ
- **КМ4** — аналог: керамогранит ректифицированный под травертин, матовый, 600×600×9 мм
- **КМ5** — керамогранит · A8UZ
- **КМ6** — аналог: наливной полимерный пол (эпоксидный), с кварцевой посыпкой, 3 мм
- **КМ7** — ПВХ · аналог: плинтус ПВХ влагостойкий 100 мм, серый
- **КМ8** — керамогранит · аналог: плинтус из керамогранита пола, подрезка 80 мм, верхняя кромка с запилом 45°

дерево (доска, паркет, ламинат) — рисунок досок

керамогранит, плитка, камень — сетка швов по формату

материал без кода цвета — по образцу (артикул в ведомости отделки)

К — краска, КМ — отделочный материал (тон КМ — по описанию, эталон — образец материала); кл. — класс истирания (1 — самый стойкий к мытью); LRV — светлота цвета: 0 — чёрный, 100 — белый; «≈» — ориентировочно

Перечень выкрасов на согласование

№	Код	Бренд / веер	Пом. / стена	Подложка	Формат	Статус
1	S 0804-Y30R	NCS Tikkurila	1, 5, 11, 12	ГКЛ с грунтом; МДФ под эмаль	600×1000; 300×600	к выполнению
2	No. 226	Farrow & Ball	2, 4, 6, 8, 9, 10, 13, 16, 17, 18, 19	ГКЛ с грунтом; МДФ под эмаль	600×1000; 300×600	к выполнению
3	No. 298	Farrow & Ball	2 A	ГКЛ с грунтом	600×1000	к выполнению
4	No. 105	Little Greene	2, 3, 4, 6, 7, 8, 9, 10, 13, 14, 15, 16, 17, 18, 19, 20	ГКЛ с грунтом; МДФ под эмаль	600×1000; 300×600	к выполнению
5	No. 93	Farrow & Ball	5 A	ГКЛ с грунтом	600×1000	к выполнению
6	S 7020-G10Y	NCS Tikkurila	13 A	ГКЛ с грунтом	600×1000	к выполнению
7	No. 64	Farrow & Ball	16 A	ГКЛ с грунтом	600×1000	к выполнению
8	S 3020-G30Y	NCS Tikkurila	18 A	ГКЛ с грунтом	600×1000	к выполнению
9	S 3040-Y70R	NCS Tikkurila	19 A	ГКЛ с грунтом	600×1000	к выполнению

Примечания

1. Цвет на листе и на экране — ориентир. До покраски — выкрас на объекте: не меньше А3 (или лист ГКЛ), на грунте под эту краску, не на белой шпаклёвке, в 2 слоя; на обороте — код, бренд, веер, дата. Смотреть днём и вечером, рядом с образцами пола и плитки; к основному цвету стен — ещё 2 соседних оттенка. Красить только в цвет утверждённого выкраса.
2. Краску заказывать по коду из графы «Система и код цвета» у бренда этого кода, не «аналогом» другого; весь объём одного кода — одной партией, колеруемую краску — за один проход машины.
3. Площади — те же, что в ведомости отделки (лист 91); сколько краски заказать — в спецификации отделочных материалов (лист 97).
4. Колерная карта на 2 листах: обозначения — на каждом, схема и палитра — на первом, выкрасы — на последнем.

Допущения и предложения на листе. Основа листа: размеры и контуры этажей подобраны проектировщиком по составу помещений и площадям этажей с картинки 470 px (размеры на ней не читаются); обмер и исходный проект — задание (К-1); высоты: 1-й этаж 2800 мм, мансарда 2700 мм (горизонтальная часть) приняты; скаты кровли мансарды приняты по картинке: колено 1200 мм, уклон 45°, конёк вдоль длинной стороны; проект КР — задание (К-2); наружные стены 400 мм, перегородки 120 мм приняты (К-1); разрешённая мощность 15 кВт принята по типовым ТУ для частного дома (К-4); подрайон климата не задан — принят не северный (жилые от 2,5 м) (К-7). Знак «*» — принято, не замерено (замерить): К-13: пол пом. 11, 12. Знак «**» — предложено, не утверждено (согласовать): плинтус пом. 1, 2, 4–14, 16, 17, фартук пом. 1, пол пом. 3, 10, 15, 20, акцент пом. 5. См. лист открытых вопросов (лист 8, записи К-1, К-2, К-4, К-7; лист 9, запись К-13).

Изм.	Кол.уч	Лист	№ док.	Подп.	Дата
Разраб.		Кырлан А.С.			04.11.26
Пров.					
ГИП					
Н. контр.					
Утв.					

ГД-2026-010-АИ

Дом 331 м²

Общая площадь 270,67* м² · * размеры приняты, не замерены (реестр — л. 8–10, К-1)

Дизайн-проект интерьера

Стадия	Лист	Листов
РП	96	216

Колерная карта

М б/м

Кырлан Александр Сергеевич

выпуск 04.11.2026 № 2a77323a49 · стр. 98 из 221

Спецификация отделочных материалов

ПРЕДВАРИТЕЛЬНО · не для производства работ · открыто пунктов: 15 (реестр — л. 8–10)

Форма 1 по ГОСТ 21.110-2013 · количества — из геометрии проекта, с запасом · часть 1 из 2

Поз.	Наименование и техническая характеристика	Тип, марка, обозначение документа	Код продукции	Поставщик	Ед. изм.	Кол.	Масса 1 ед., кг	Примечание
	Лакокрасочные материалы							
1	Краска интерьерная водно-дисперсионная акриловая для стен, полуматовая, класс мокрого истирания 1 по EN 13300, база A; цвет NCS S 0804-Y30R «S 0804-Y30R», колеровка машинная	Tikkurila Luja 7		Tikkurila	л	30,6		поз. К1 колерной карты; пом. 1, 11, 12; S = 113,2 м² × 2 сл. × 0,12 л/м² = 27,2 л, +10 % и 0,5 л на подкраску → ≥ 30,4 л; тара 3 × 9 л + 1 × 2,7 л + 1 × 0,9 л
2	Краска интерьерная водно-дисперсионная акриловая для потолков, матовая, класс мокрого истирания 1 по EN 13300, база A; цвет NCS S 0804-Y30R «S 0804-Y30R», колеровка машинная	Tikkurila Luja 7		Tikkurila	л	14,4		поз. К2 колерной карты; пом. 1, 11, 12; S = 49,8 м² × 2 сл. × 0,12 л/м² = 12,0 л, +10 % и 0,5 л на подкраску → ≥ 13,6 л; тара 1 × 9 л + 2 × 2,7 л
3	Краска интерьерная водно-дисперсионная акриловая для стен, матовая, класс мокрого истирания 1 по EN 13300, база A; цвет по вееру Farrow & Ball No. 226 «Joa's White», колеровка машинная	Farrow & Ball Modern Emulsion		Farrow & Ball	л	87,5		поз. К4 колерной карты; пом. 2, 4, 6, 8, 9, 10, 13, 16, 17, 18, 19; S = 325,9 м² × 2 сл. × 0,12 л/м² = 78,2 л, +10 % и 0,5 л на подкраску → ≥ 86,5 л; тара 17 × 5 л + 1 × 2,5 л
4	Краска интерьерная водно-дисперсионная акриловая для акцентных стен, матовая, класс мокрого истирания 1 по EN 13300, база C; цвет по вееру Farrow & Ball No. 298 «Bancha», колеровка машинная	Farrow & Ball Modern Emulsion		Farrow & Ball	л	2,5		поз. К5 колерной карты; пом. 2; S = 5,7 м² × 2 сл. × 0,12 л/м² = 1,4 л, +10 % и 0,5 л на подкраску → ≥ 2,0 л; тара 1 × 2,5 л
5	Краска интерьерная водно-дисперсионная акриловая для потолков, глубокоматовая, класс мокрого истирания 2 по EN 13300, база A; цвет по вееру Little Greene No. 105 «Slaked Lime», колеровка машинная	Little Greene Absolute Matt		Little Greene	л	54,1		поз. К6 колерной карты; пом. 2, 4, 6, 7, 8, 9, 10, 13, 14, 16, 17, 18, 19; S = 202,9 м² × 2 сл. × 0,12 л/м² = 48,7 л, +10 % и 0,5 л на подкраску → ≥ 54,1 л; тара — кратно фасовке продукта
6	Краска интерьерная водно-дисперсионная акриловая для потолков, матовая, класс мокрого истирания 1 по EN 13300, база A; цвет по вееру Little Greene No. 105 «Slaked Lime», колеровка машинная	Little Greene Intelligent Bathroom		Little Greene	л	6,1		поз. К8 колерной карты; пом. 3, 15, 20; S = 20,9 м² × 2 сл. × 0,12 л/м² = 5,0 л, +10 % и 0,5 л на подкраску → ≥ 6,0 л; тара — кратно фасовке продукта
7	Краска интерьерная водно-дисперсионная акриловая для стен, матовая, класс мокрого истирания 2 по EN 13300, база A; цвет NCS S 0804-Y30R «S 0804-Y30R», колеровка машинная	Tikkurila Optiva 5 Matt		Tikkurila	л	9,9		поз. К9 колерной карты; пом. 5; S = 32,2 м² × 2 сл. × 0,12 л/м² = 7,7 л, +10 % и 0,5 л на подкраску → ≥ 9,0 л; тара 1 × 9 л + 1 × 0,9 л
8	Краска интерьерная водно-дисперсионная акриловая для акцентных стен, матовая, класс мокрого истирания 1 по EN 13300, база C; цвет по вееру Farrow & Ball No. 93 «Studio Green — почти чёрный зелёный», колеровка машинная	Farrow & Ball Modern Emulsion		Farrow & Ball	л	7,5		поз. К10 колерной карты; пом. 5; S = 12,9 м² × 3 сл. × 0,12 л/м² = 4,7 л, +10 % и 0,5 л на подкраску → ≥ 5,6 л; тара 1 × 5 л + 1 × 2,5 л
9	Краска интерьерная водно-дисперсионная акриловая для потолков, глубокоматовая, класс мокрого истирания 2 по EN 13300, база A; цвет NCS S 0804-Y30R «S 0804-Y30R», колеровка машинная	Tikkurila Anti-Reflex 2		Tikkurila	л	9,9		поз. К11 колерной карты; пом. 5; S = 33,7 м² × 2 сл. × 0,12 л/м² = 8,1 л, +10 % и 0,5 л на подкраску → ≥ 9,4 л; тара 1 × 9 л + 1 × 0,9 л
10	Краска интерьерная водно-дисперсионная акриловая для стен, матовая, класс мокрого истирания 1 по EN 13300, база A; цвет по вееру Little Greene No. 105 «Slaked Lime», колеровка машинная	Little Greene Intelligent Matt		Little Greene	л	11,6		поз. К12 колерной карты; пом. 7, 14; S = 42,0 м² × 2 сл. × 0,12 л/м² = 10,1 л, +10 % и 0,5 л на подкраску → ≥ 11,6 л; тара — кратно фасовке продукта
11	Краска интерьерная водно-дисперсионная акриловая для акцентных стен, матовая, класс мокрого истирания 2 по EN 13300, база C; цвет NCS S 7020-G10Y «Хвойный тёмно-зелёный», колеровка машинная	Tikkurila Optiva 5 Matt		Tikkurila	л	2,7		поз. К14 колерной карты; пом. 13; S = 7,6 м² × 2 сл. × 0,12 л/м² = 1,8 л, +10 % и 0,5 л на подкраску → ≥ 2,5 л; тара 1 × 2,7 л
12	Краска интерьерная водно-дисперсионная акриловая для акцентных стен, матовая, класс мокрого истирания 1 по EN 13300, база C; цвет по вееру Farrow & Ball No. 64 «Red Earth», колеровка машинная	Farrow & Ball Modern Emulsion		Farrow & Ball	л	2,5		поз. К15 колерной карты; пом. 16; S = 7,3 м² × 2 сл. × 0,12 л/м² = 1,8 л, +10 % и 0,5 л на подкраску → ≥ 2,4 л; тара 1 × 2,5 л
13	Краска интерьерная водно-дисперсионная акриловая для акцентных стен, матовая, класс мокрого истирания 2 по EN 13300, база C; цвет NCS S 3020-G30Y «S 3020-G30Y», колеровка машинная	Tikkurila Optiva 5 Matt		Tikkurila	л	4,5		поз. К16 колерной карты; пом. 18; S = 12,3 м² × 2 сл. × 0,12 л/м² = 3,0 л, +10 % и 0,5 л на подкраску → ≥ 3,8 л; тара 1 × 2,7 л + 2 × 0,9 л
14	Краска интерьерная водно-дисперсионная акриловая для акцентных стен, матовая, класс мокрого истирания 2 по EN 13300, база C; цвет NCS S 3040-Y70R «S 3040-Y70R», колеровка машинная	Tikkurila Optiva 5 Matt		Tikkurila	л	4,5		поз. К18 колерной карты; пом. 19; S = 14,8 м² × 2 сл. × 0,12 л/м² = 3,6 л, +10 % и 0,5 л на подкраску → ≥ 4,4 л; тара 1 × 2,7 л + 2 × 0,9 л
15	Акрилово-уретановая эмаль на водной основе, полуглянцевая в цвет NCS S 0804-Y30R «S 0804-Y30R» — окраска плинтуса	аналог по характеристикам			л	1		поз. К3; пом. 1, 5; L = 36,5 м, S = 3,5 м² × 2 сл. × 0,12 л/м² + 10 %; продукт подобрать в веере NCS
16	Краска для МДФ и дерева в цвет Farrow & Ball No. 226 «Joa's White» — окраска плинтуса; блеск не ниже блеска стен	марка не задана			л	3,2		поз. К7, К17; пом. 2, 4, 6, 8, 9, 13, 16, 17, 18, 19; L = 127,7 м, S = 11,9 м² × 2 сл. × 0,12 л/м² + 10 %; продукт подобрать в веере Farrow & Ball
17	Краска для МДФ и дерева в цвет Little Greene No. 105 «Slaked Lime» — окраска плинтуса; блеск не ниже блеска стен	марка не задана			л	0,5		поз. К13; пом. 7, 14; L = 16,8 м, S = 1,6 м² × 2 сл. × 0,12 л/м² + 10 %; продукт подобрать в веере Little Greene
18	Грунтовка акриловая под окраску стен и потолков — из системы производителя краски	по системе краски			м²	882		площадь окраски стен, акцентов и потолков; 1 слой перед окраской; расход — по ТУ грунтовки

Допущения и предложения на листе

Основа листа: размеры и контуры этажей подобраны проектировщиком по составу помещений и площадям этажей с картинки 470 px (размеры на ней не читаются); обмер и исходный проект — задание (К-1); высоты: 1-й этаж 2800 мм, мансарда 2700 мм (горизонтальная часть) приняты; скаты кровли мансарды приняты по картинке: колено 1200 мм, уклон 45°, конёк вдоль длинной стороны; проект КР — задание (К-2); наружные стены 400 мм, перегородки 120 мм приняты (К-1); разрешённая мощность 15 кВт принята по типовым ТУ для частного дома (К-4); подрайон климата не задан — принят не северный (жилые от 2,5 м) (К-7).

Знак «*» — принято, не замерено и не подтверждено (замерить на объекте): К-13: пол пом. 11, 12 — отметка верха плиты −0,170 принята по пирогу (плита веранды и крыльца своя, ниже плиты дома) — подтвердить по проекту КР или обмером (К-13).

Знак «**» — предложение проектировщика, заказчиком не утверждено (согласовать с заказчиком): плинтус пом. 1, 2, 4–14, 16, 17, фартук пом. 1, акцент пом. 5 — артикул изделия не выбран: позиция описана характеристиками («аналог по характеристикам»), артикул выбирается при закупке; пол пом. 3, 15, 20 — пирог пола: стяжка 33 мм и обмазочная гидроизоляция добавлены разработчиком проекта; артикул изделия не выбран: позиция описана характеристиками («аналог по характеристикам»), артикул выбирается при закупке; пол пом. 10 — покрытие пола гаража — предложение исполнителя: выдерживает шины, масло и антигололёдные реагенты, без швов.

См. лист открытых вопросов (лист 8, записи К-1, К-2, К-4, К-7; лист 9, запись К-13).

Изм.	Кол.уч	Лист	№ док.	Подп.	Дата
Разраб.		Кырлан А.С.			04.11.26
Пров.					
ГИП					
Н. контр.					
Утв.					

ГД-2026-010-АИ

Дом 331 м²

Общая площадь 270,67* м² · * размеры приняты, не замерены (реестр — л. 8–10, К-1)

Дизайн-проект интерьера	Стадия	Лист	Листов
	РП	97	216

Спецификация отделочных материалов

М б/м

Кырлан Александр Сергеевич

выпуск 04.11.2026 № 2a77323849 · стр. 99 из 221

Спецификация отделочных материалов

Форма 1 по ГОСТ 21.110-2013 · количества — из геометрии проекта, с запасом · часть 2 из 2

ПРЕДВАРИТЕЛЬНО · не для производства работ · открыто пунктов: 15 (реестр — л. 8–10)

Поз.	Наименование и техническая характеристика	Тип, марка, обозначение документа	Код продукции	Поставщик	Ед. изм.	Кол.	Масса 1 ед., кг	Примечание
	Плитка и керамогранит							
19	Керамогранит под травертин, 600×600×9 мм, ректификат, водопоглощение 0,1 % (BIa), противоскольжение R10, PEI IV	аналог по характеристикам			м²	22,32		шов 2 мм; Санузел 1 этажа, пол; Санузел мастер, пол; Санузел 2, пол; по раскладке 56 шт (S = 18,04 м²), с запасом 62 шт
20	A8UZ, 600×1200×9 мм, ректификат, водопоглощение 0,1 % (BIa), противоскольжение R10, PEI IV	A8UZ		Atlas Concorde	м²	163,44		шов 2 мм; Санузел 1 этажа, стены А–Г; Санузел 1 этажа, короб инсталляции; Санузел мастер, стены А–Г; Санузел мастер, короб инсталляции; Санузел 2, стены А–Г; Санузел 2, короб инсталляции; Котельная, пол; Прихожая, пол; Тамбур, пол; Веранда, пол; Крыльцо, пол; по раскладке 202 шт (S = 108,61 м²), с запасом 227 шт
21	Керамогранит матовый, тон F497, ректификат, водопоглощение 0,5 % (BIa)	аналог по характеристикам			м²	1,26		1. Кухня-столовая, фартук; раскладка не выполнена — S = 1,15 м² + 10 %; клей и затирка — по раскладке
22	Плинтус из керамогранита пола, подрезка 80 мм, верхняя кромка с запилом 45°	аналог по характеристикам			м²	22,53		11. Веранда, стены; раскладка не выполнена — S = 20,48 м² + 10 %; клей и затирка — по раскладке
23	Плинтус из керамогранита пола, подрезка 80 мм, верхняя кромка с запилом 45°	аналог по характеристикам			м²	7		12. Крыльцо, стены; раскладка не выполнена — S = 6,36 м² + 10 %; клей и затирка — по раскладке
	Напольные покрытия							
24	1167-4250, рабочий слой 4 мм, эмиссия E1, укладка на клей	1167-4250		Coswick	м²	201,4		пом. 1, 2, 5, 6, 7, 13, 14, 16, 17, 18, 19; S = 188,22 м² + 7 % (прямая укладка); к заказу — кратно упаковке
25	Клей для паркета и инженерной доски, эластичный (СМП / полиуретановый)	по рекомендации производителя доски			м²	189		площадь приклейки; расход и шпатель — по ТУ клея
	Погонажные изделия							
26	Плинтус МДФ под окраску 80×16 мм, крепление к стене, окраска в цвет NCS S 0804-Y30R	аналог по характеристикам			м	41		пом. 1, 5; L = 36,5 м (периметр без дверных проёмов) + 10 % на подрезку; в штуках — по длине планки
27	Плинтус МДФ под покраску 80×16, крепление к стене, окраска в цвет Farrow & Ball No. 226	аналог по характеристикам			м	106		пом. 2, 4, 6, 8, 9, 13, 16, 17; L = 95,5 м (периметр без дверных проёмов) + 10 % на подрезку; в штуках — по длине планки
28	Плинтус МДФ под покраску 80×16, крепление к стене, окраска в цвет Little Greene No. 105	аналог по характеристикам			м	19		пом. 7, 14; L = 16,8 м (периметр без дверных проёмов) + 10 % на подрезку; в штуках — по длине планки
29	Плинтус ПВХ влагостойкий 100 мм, серый, h = 100 мм, крепление к стене	аналог по характеристикам			м	25		пом. 10; L = 22,0 м (периметр без дверных проёмов) + 10 % на подрезку; в штуках — по длине планки
30	Плинтус из керамогранита пола, подрезка 80 мм, верхняя кромка с запилом 45°, h = 80 мм, крепление к стене	аналог по характеристикам			м	30		пом. 11, 12; L = 26,8 м (периметр без дверных проёмов) + 10 % на подрезку; в штуках — по длине планки
31	SX165, h = 69 мм, крепление к стене, окраска в цвет Farrow & Ball No. 226	SX165		Orac Decor	м	36		пом. 18, 19; L = 32,2 м (периметр без дверных проёмов) + 10 % на подрезку; в штуках — по длине планки
	Смеси и материалы для облицовки							
32	Затирка для швов плитки, класс CG2WA по EN 13888	Mapei Ultracolor Plus 132		Mapei	кг	11		по раскладке (a+b)/(a·b) × шов × t × 1,6 + 10 %; в т. ч. 3,9 кг — позиции раскладки без марки
33	Клей плиточный C2 TE S1 по EN 12004, слой 5 мм	Ceresit CM 17		Ceresit	кг	1080		44 меш. по 25 кг; 1,5 кг/м² на 1 мм слоя + 10 %; в т. ч. 389 кг — позиции раскладки без марки
34	Гидроизоляция обмазочная мокрых зон: пол, стены по периметру, зоны замачивания; 2 слоя с армирующей лентой в углах	аналог по характеристикам			м²	44,9		площадь по листу раскладки плитки + 10 %; расход смеси — по ТУ
35	Лента демпферная по периметру пола из плитки	аналог по характеристикам			м	90,5		периметр без дверных проёмов + 10 %

Примечания

1. Количества — из геометрии проекта: площади поверхностей по чистым граням стен до отделки (те же, что в ведомости отделки и колерной карте), плитка, клей и затирка — по раскладке плиточника; в графе «Кол.» — к заказу, с запасом.
2. Краска: расход 0,12 л/м² на слой в 2 слоя, если по ТУ не задан иной; запас 10 % и 0,5 л на подкраску каждого кода. Один код — одна партия, колеровка машинная в колеровочном центре бренда; в заказ — только после утверждения выкраса (колерная карта). Фасовка — по каталогу бренда на дату выпуска; к заказу — не меньше расчётного объёма.
3. «Аналог по характеристикам» — допускается изделие другого производителя с характеристиками не ниже указанных, по согласованию с автором проекта.
4. Графы «Код продукции» и «Масса 1 ед.» не заполнены: коды по классификатору продукции не присвоены, масса единицы до 25 кг (ГОСТ 21.110-2013).
5. Грунтовка и клей для доски указаны площадью обработки; объём — по ТУ выбранного продукта.

Допущения и предложения на листе

Основа листа: размеры и контуры этажей подобраны проектировщиком по составу помещений и площадям этажей с картинки 470 px (размеры на ней не читаются); обмер и исходный проект — задание (К-1); высоты: 1-й этаж 2800 мм, мансарда 2700 мм (горизонтальная часть) приняты; скаты кровли мансарды приняты по картинке: колено 1200 мм, уклон 45°, конёк вдоль длинной стороны; проект КР — задание (К-2); наружные стены 400 мм, перегородки 120 мм приняты (К-1); разрешённая мощность 15 кВт принята по типовым ТУ для частного дома (К-4); подрайон климата не задан — принят не северный (жилые от 2,5 м) (К-7).

Знак «*» — принято, не замерено и не подтверждено (замерить на объекте): К-13: пол пом. 11, 12 — отметка верха плиты −0,170 принята по пирогу (плита веранды и крыльца своя, ниже плиты дома) — подтвердить по проекту КР или обмером (К-13).

Знак «**» — предложение проектировщика, заказчиком не утверждено (согласовать с заказчиком): плинтус пом. 1, 2, 4–14, 16, 17, фартук пом. 1, акцент пом. 5 — артикул изделия не выбран: позиция описана характеристиками («аналог по характеристикам»), артикул выбирается при закупке; пол пом. 3, 15, 20 — пирог пола: стяжка 33 мм и обмазочная гидроизоляция добавлены разработчиком проекта; артикул изделия не выбран: позиция описана характеристиками («аналог по характеристикам»), артикул выбирается при закупке; пол пом. 10 — покрытие пола гаража — предложение исполнителя: выдерживает шины, масло и антигололёдные реагенты, без швов.

См. лист открытых вопросов (лист 8, записи К-1, К-2, К-4, К-7; лист 9, запись К-13).

Изм.	Кол.уч	Лист	№ док.	Подп.	Дата
Разраб.		Кырлан А.С.			04.11.26
Пров.					
ГИП					
Н. контр.					
Утв.					

ГД-2026-010-АИ

Дом 331 м²

Общая площадь 270,67* м² · * размеры приняты, не замерены (реестр — л. 8–10, К-1)

Дизайн-проект интерьера	Стадия	Лист	Листов
	РП	98	216
Спецификация отделочных материалов М б/м	**Кырлан Александр Сергеевич**		

Концепция декора и визуализации

Шале · визуализации, палитра, материалы, ключевые предметы



Визуализация 1. Вид сверху (3D): планировка с мебелью, текстилем и декором

Расстановка — по плану мебели (лист 30); шторы, ковры, картины и растения — по плану текстиля и декора (лист 100).




Визуализация 22. Гостиная (пом. 5)

шторы Т1, Т2 · ковёр Т3 · картина ДК1 · растение ДК2, ДК21 · подушки, пледы Т4, Т5, Т6



Визуализация 20. Кухня-столовая (пом. 1)

шторы Т14 · растение ДК9

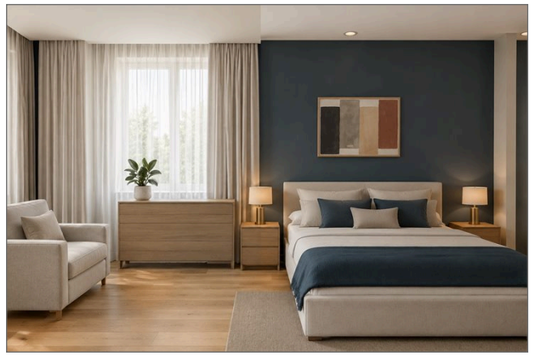

Визуализация 8. Спальня мастер (пом. 13)

шторы Т13, Т15 · ковёр Т16 · картина ДК4 · растение ДК27 · подушки, пледы Т17, Т18, Т19



Визуализация 10. Спальня 2 (пом. 16)

шторы Т20, Т21 · ковёр Т22 · картина ДК6 · зеркало ДК7 · подушки, пледы Т23, Т24, Т25

Материалы и фактуры



Дуб натуральный

пол: пом. 1, 2, 5, 6, 7, 13, 14, 16, 17, 18, 19; рамы ДК3, ДК4,



Травертин (керамогранит)

пол и стены санузлов, фартук: пом. 3, 15, 20



Букле

подушки: Т10, Т23, Т29, Т35



Лён

рулонная, портьеры, подушки: Т1, Т4, Т14, Т20, Т26, Т32, Т40, Т41



Бронза и чёрный металл

рамы ДК5, ДК7, ДК11, ДК13 чёрный; фурнитура, светильники

Ключевые предметы

— Диван Кб3 2000×900 — кабинет-гостевая; подушки и плед Т10, Т11, Т12
— Диван Гс2 3200×1000 — гостиная; подушки и плед Т4, Т5, Т6
— Диван Вр2 2000×800 — веранда
— Кровати Дт1, Дт4, М1, С1 — над изголовьем картины ДК4, ДК6, ДК10, ДК12; текстиль Т17, Т18, Т19, Т23, Т24, Т25, Т29, Т30, Т31, Т35, Т36, Т37
— Ковры Т3, Т9, Т16, Т22, Т28, Т34, Т40, Т41 — джут плетёный, шерсть с джутом, резиновая крошка SBR с цветными EPDM-вкраплениями, шерсть, TPE, хлопок
— Картины ДК1, ДК3, ДК4, ДК6, ДК10, ДК12 — центр на высоте 1450–1650 мм
— Зеркала в рост ДК5, ДК7, ДК11, ДК31; над умывальниками ДК13
— Шторы-волна Т1, Т7, Т13, Т20, Т26, Т32 (Farrow & Ball No. 40), тюль Т2, Т8, Т15, Т21, Т27, Т33 (NCS S 0804-Y30R) — в нишах потолка

Настроение

Современное шале 60 % + эко 40 %: загородный дом у леса. Стены — шерстяной белый Joa's White No. 226 и молочный S 0804-Y30R, потолки — известковый Slaked Lime No. 105; второй план — выцветший оливковый V451, шалфей S 3020-G30Y, песчаник X463; акценты — хвойный S 7020-G10Y, терракота Red Earth No. 64, брусника Eating Room Red No. 43. Дерево — дуб и лиственница под маслом, камень у камина. Настроение стиля: защищённый, тёплый, основательный, природный, камерный, после мороза — у огня. Свет тёплый, 2200–2700 K.

Примечания

1. Визуализации — образ интерьера. Изделия, размеры, высоты подвеса и привязки — по чертежам (план текстиля и декора — лист 100; шторы и карнизы — лист 102; ведомость текстиля — лист 103; ведомость декора и развеса — лист 105); при расхождении действуют чертежи и ведомости.
2. Коды цвета — ориентир подбора по веерам производителей; ткань утверждается по образцу при дневном свете и при свете проекта 2700–3000 K.
3. Мелкий стайлинг на визуализациях (книги, посуда, свечи) в ведомости не входит и поставляется заказчиком по желанию.

Палитра 60/30/10 и цвета текстиля



- Farrow & Ball No. 226 (Joa's White), LRV 63 — 60 % база — Т4, Т33
- Little Greene No. 105 (Slaked Lime), LRV 82 — 60 % база — Т15, Т21
- NCS S 3020-G30Y (шалфей), LRV 38 — 30 % второй цвет — Т30, Т31, Т41
- Farrow & Ball No. 229 (Elephant's Breath — тёплый средне-серый с лиловым подтоном), LRV 52 — 30 % второй цвет — Т13
- Farrow & Ball No. 243 (Charleston Gray — серо-коричневый «камень»), LRV 30 — 30 % второй цвет — Т3, Т40
- NCS S 0804-Y30R (тёплый молочный белый), LRV 85 — 60 % база — Т2, Т8, Т27
- Tikkurila V451 (выцветший оливковый), LRV 51 — 30 % второй цвет — Т26, Т29
- Tikkurila X463 (бежевый песчаник), LRV 51 — 30 % второй цвет — Т9, Т20, Т23, Т35
- Farrow & Ball No. 40 (Mouse's Back — тёплый коричнево-серый), LRV 26 — 30 % второй цвет — Т7
- NCS S 2005-Y20R (Светлый песочно-серый), LRV 60 — 30 % второй цвет — Т1, Т14, Т16, Т17, Т28, Т32

Допущения и предложения на листе. Основа листа: размеры и контуры этажей подобраны проектировщиком по составу помещений и площадям этажей с картинки 470 px (размеры на ней не читаются); обмер и исходный проект — задание (К-1); высоты: 1-й этаж 2800 мм, мансарда 2700 мм (горизонтальная часть) приняты; скаты кровли мансарды приняты по картинке: колено 1200 мм, уклон 45°, конёк вдоль длинной стороны; проект КР — задание (К-2); наружные стены 400 мм, перегородки 120 мм приняты (К-1); разрешённая мощность 15 кВт принята по типовым ТУ для частного дома (К-4); подрайон климата не задан — принят не северный (жилые от 2,5 м) (К-7). См. лист открытых вопросов (лист 8, записи К-1, К-2, К-4, К-7).

Изм.	Кол.уч	Лист	№ док.	Подп.	Дата
Разраб.		Кырлан А.С.			04.11.26
Пров.					
ГИП					
Н. контр.					
Утв.					

ГД-2026-010-АИ

Дом 331 м²

Общая площадь 270,67* м² · * размеры приняты, не замерены (реестр — л. 8–10, К-1)

Дизайн-проект интерьера

Стадия	Лист	Листов
РП	99	216

Концепция декора и визуализации

М б/м


Кырлан Александр Сергеевич

выпуск 04.11.2026 № 2a77323a49 · стр. 101 из 221

План текстиля и декора · 1-й этаж

Шторы и карнизы, ковры, картины и зеркала, растения · размеры в мм от чистовых стен и чистого пола · марки — по ведомостям

ПРЕДВАРИТЕЛЬНО · не для производства работ · открыто пунктов: 15 (реестр — л. 8–10)

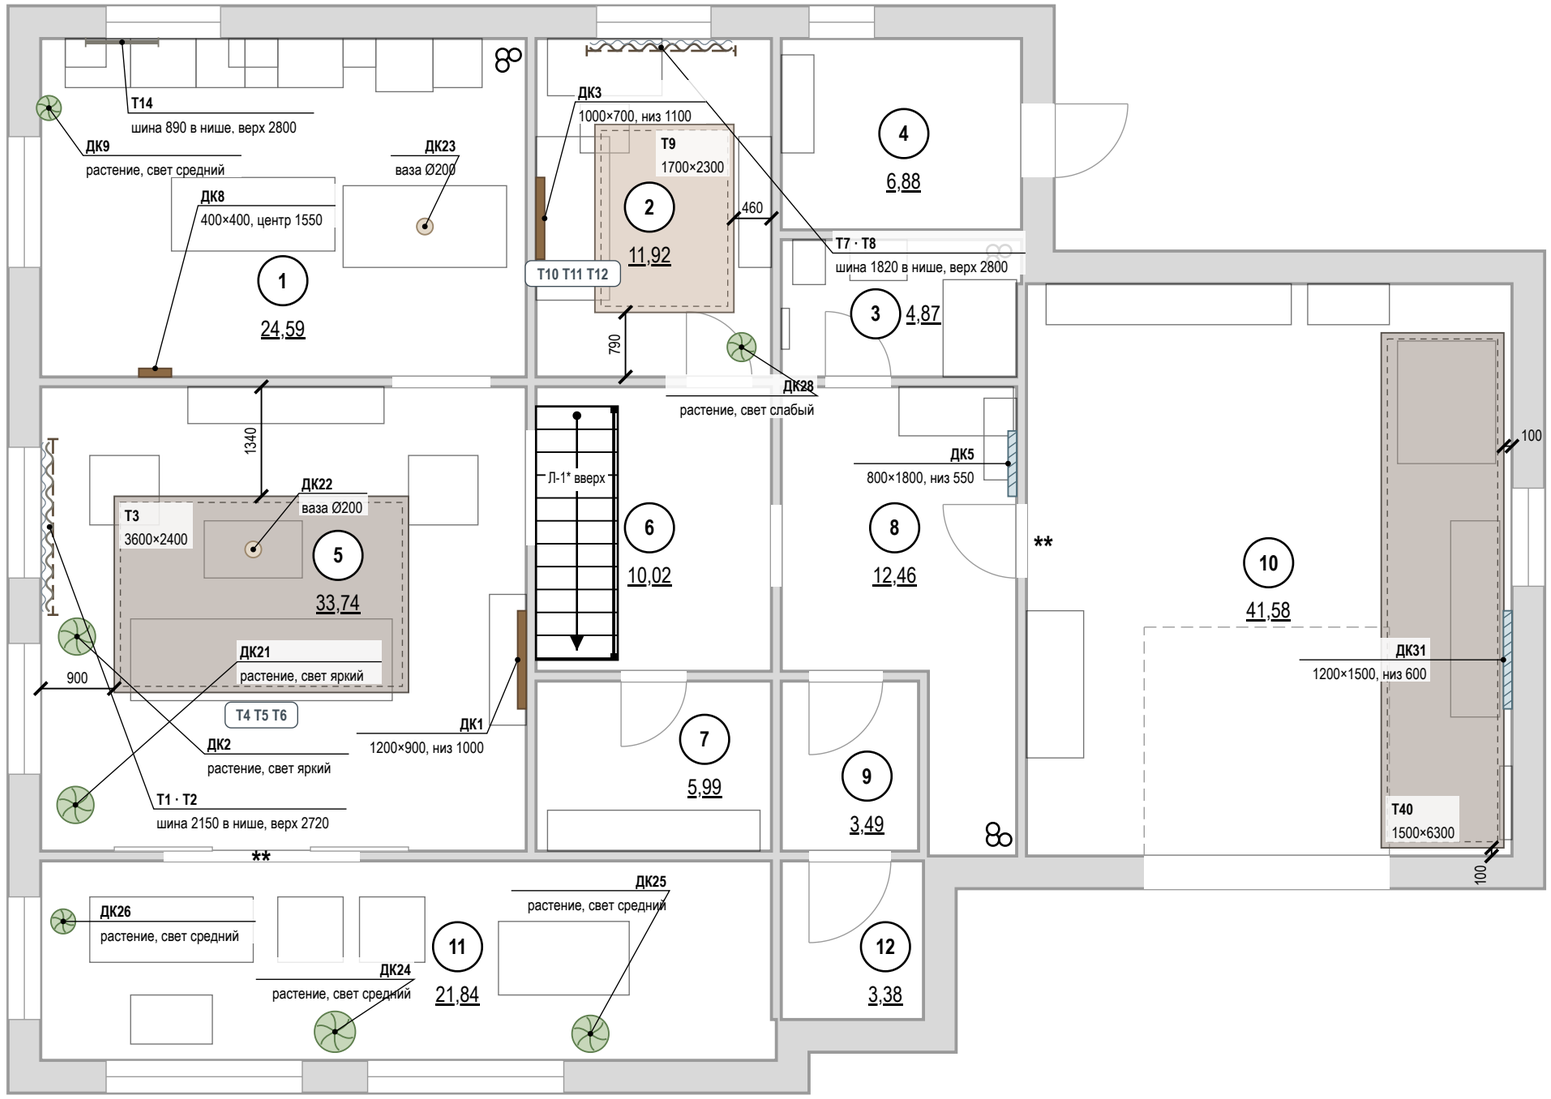

Условные обозначения

- ковёр — габарит в масштабе, цвет изделия
- шина или карниз штор (выше плоскости разреза)
- портьеры (штора-волна)
- тюль (на плане — волнистая линия)
- римская или рулонная штора в проёме
- картина на стене — ширина в масштабе
- зеркало на стене — ширина в масштабе
- растение в кашпо — диаметр в масштабе
- ваза, настольный декор
- подушки, пледы — марки на мебели
- привязка от чистовой стены, мм
- (1) номер помещения, площадь м²
- стены (подложка обмера)
- ** «**» — предложение проектировщика, заказчиком не утверждено

Т1, ДК1 — марки по ведомостям текстиля и декора

Экспликация помещений

лист 19 · на плане — номера в марках

Окна: шина → полотно, мм

Поз.	Шина	Верх шины	Полотно, низ
Т14	890	2800, ниша	2000, низ 800
Т7, Т8	1820	2800, ниша	2790, низ 10
Т1, Т2	2150	2720, ниша	2710, низ 10

Развеска: высоты от пола, мм

Поз.	Пом.	Ш×В	Центр	Низ	Стена
ДК1	5	1200×900	1450	1000	Б
ДК3	2	1000×700	1450	1100	Г
ДК5	8	800×1800	1450	550	Б
ДК8	1	400×400	1550	1350	В
ДК31	10	1200×1500	1350	600	Б

Допущения и предложения на листе. Основа листа: размеры и контуры этажей подобраны проектировщиком по составу помещений и площадям этажей с картинки 470 px (размеры на ней не читаются); обмер и исходный проект — задание (К-1); высоты: 1-й этаж 2800 мм, мансарда 2700 мм (горизонтальная часть) приняты; скаты кровли мансарды приняты по картинке: колено 1200 мм, уклон 45°, конёк вдоль длинной стороны; проект КР — задание (К-2); наружные стены 400 мм, перегородки 120 мм приняты (К-1); разрешённая мощность 15 кВт принята по типовым ТУ для частного дома (К-4); подрайон климата не задан — принят не северный (жилые от 2,5 м) (К-7). Знак «*» — принято, не замерено (замерить): К-6: Л-1. Знак «**» — предложено, не утверждено (согласовать). См. лист открытых вопросов (лист 8, записи К-1, К-2, К-4, К-6, К-7; лист 9, запись К-9).

Примечания

1. Размеры — в мм. Отступы ковров — от чистовых стен; высоты картин и зеркал — от чистого пола до центра или низа рамы.
2. Шторы — на шинах в нишах потолка (ниша — план потолков, лист 73); закладная под шину — до обшивки ГКЛ. Схемы окон, длины полотен и сборка — лист 102.
3. Картины и зеркала массой более 5 кг — на анкеры по основанию, нагрузка крепежа не меньше двойной массы изделия; на ГКЛ — только по закладной. Декор не перекрывает розетки и выключатели.
4. Ковры на гладком полу — на противоскользящей подложке.
5. Мебель — по плану расстановки мебели (лист 30); ведомость текстиля — лист 103, ведомость декора и схемы развески — лист 105.
6. Номера помещений — по экспликации (лист 19); наименования и площади на этом листе не дублируются.
7. Марки текстиля «Т» и декора «Д» относятся только к листам текстиля и декора; индексы трубопроводов Т1–Т4 — на листах ВК и ОВ.

1000 мм · печать 1:1

Изм.	Кол.уч	Лист	№ док.	Подп.	Дата
Разраб.		Кырлан А.С.			04.11.26
Пров.					
ГИП					
Н. контр.					
Утв.					

ГД-2026-010-АИ

Дом 331 м²

Общая площадь 270,67* м² · * размеры приняты, не замерены (реестр — л. 8–10, К-1)

Дизайн-проект интерьера

Стадия	Лист	Листов
РП	100	216

План текстиля и декора · 1-й этаж

М 1:75


Кырлан Александр Сергеевич

выпуск 04.11.2026 № 2a77323a49 · стр. 102 из 221

План текстиля и декора · Мансарда

Шторы и карнизы, ковры, картины и зеркала, растения · размеры в мм от чистовых стен и чистого пола · марки — по ведомостям

ПРЕДВАРИТЕЛЬНО · не для производства работ · открыто пунктов: 15 (реестр — л. 8–10)

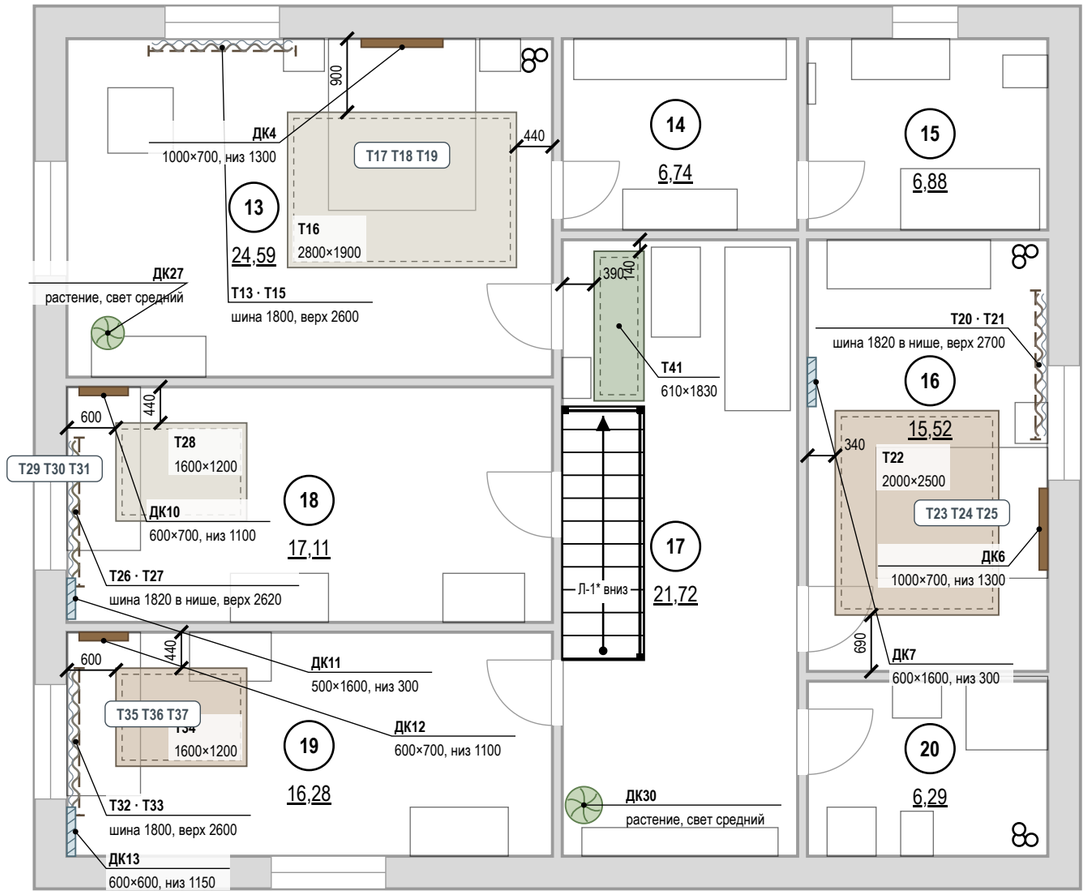

Условные обозначения

- ковёр — габарит в масштабе, цвет изделия
- шина или карниз штор (выше плоскости разреза)
- портьеры (штора-волна)
- тюль (на плане — волнистая линия)
- римская или рулонная штора в проёме
- картина на стене — ширина в масштабе
- зеркало на стене — ширина в масштабе
- растение в кашпо — диаметр в масштабе
- ваза, настольный декор
- подушки, пледы — марки на мебели
- привязка от чистовой стены, мм
- (1) номер помещения, площадь м²
- стены (подложка обмера)

Т1, ДК1 — марки по ведомостям текстиля и декора

Экспликация помещений

лист 20 · на плане — номера в марках

Окна: шина → полотно, мм

Поз.	Шина	Верх шины	Полотно, низ
T13, T15	1800	2600	2590, низ 10
T20, T21	1820	2700, ниша	2690, низ 10
T26, T27	1820	2620, ниша	2610, низ 10
T32, T33	1800	2600	2590, низ 10

Развеска: высоты от пола, мм

Поз.	Пом.	Ш×В	Центр	Низ	Стена
ДК4	13	1000×700	1650	1300	А
ДК6	16	1000×700	1650	1300	Б
ДК7	16	600×1600	1100	300	Г
ДК10	18	600×700	1450	1100	А
ДК11	18	500×1600	1100	300	Г
ДК12	19	600×700	1450	1100	А
ДК13	19	600×600	1450	1150	Г

Допущения и предложения на листе

Основа листа: размеры и контуры этажей подобраны проектировщиком по составу помещений и площадям этажей с картинки 470 px (размеры на ней не читаются); обмер и исходный проект — задание (К-1); высоты: 1-й этаж 2800 мм, мансарда 2700 мм (горизонтальная часть) приняты; скаты кровли мансарды приняты по картинке: колено 1200 мм, уклон 45°, конёк вдоль длинной стороны; проект КР — задание (К-2); наружные стены 400 мм, перегородки 120 мм приняты (К-1); разрешённая мощность 15 кВт принята по типовым ТУ для частного дома (К-4); подрайон климата не задан — принят не северный (жилые от 2,5 м) (К-7).

Знак «*» — принято, не замерено и не подтверждено (замерить на объекте): К-2: отметка чистого пола этажа «Мансарда» +3,150 — принята без источника, все отметки мансарды считаются от неё; К-6: Л-1 — габарит марша снят с картинки заказчика (11 проступей в холле 3,6 м), а до отм. +3,150 нужно 18 подъёмов — одномаршевая не встаёт: решение по К-6.

См. лист открытых вопросов (лист 8, записи К-1, К-2, К-4, К-6, К-7).

Примечания

1. Размеры — в мм. Отступы ковров — от чистовых стен; высоты картин и зеркал — от чистого пола до центра или низа рамы.
2. Шторы — на шинах в нишах потолка (ниша — план потолков, лист 73); закладная под шину — до обшивки ГКЛ. Схемы окон, длины полотен и сборка — лист 102.
3. Картины и зеркала массой более 5 кг — на анкеры по основанию, нагрузка крепежа не меньше двойной массы изделия; на ГКЛ — только по закладной. Декор не перекрывает розетки и выключатели.
4. Ковры на гладком полу — на противоскользящей подложке.
5. Мебель — по плану расстановки мебели (лист 30); ведомость текстиля — лист 103, ведомость декора и схемы развески — лист 105.
6. Номера помещений — по экспликации (лист 20); наименования и площади на этом листе не дублируются.
7. Марки текстиля «Т» и декора «Д» относятся только к листам текстиля и декора; индексы трубопроводов Т1–Т4 — на листах ВК и ОВ.

1000 мм · печать 1:1

Изм.	Кол.уч	Лист	№ док.	Подп.	Дата
Разраб.		Кырлан А.С.			04.11.26
Пров.					
ГИП					
Н. контр.					
Утв.					

ГД-2026-010-АИ

Дом 331 м²

Общая площадь 270,67* м² · * размеры приняты, не замерены (реестр — л. 8–10, К-1)

Дизайн-проект интерьера

Стадия	Лист	Листов
РП	101	216

План текстиля и декора · Мансарда

М 1:75

Кырлан Александр Сергеевич

выпуск 04.11.2026 № 2a77323a49 · стр. 103 из 221

03

Декор и текстиль


Кырлан Александр Сергеевич

выпуск 04.11.2026 № 2a77323a49 · стр. 104 из 221


Шторы и карнизы

Схемы окон «шина → полотно» (М 1:100) · отметки в м от ±0,000 (чистый пол 1-го этажа) · размеры в мм


Окно 1 — Кухня-столовая (пом. 1): Т14 (М 1:100)

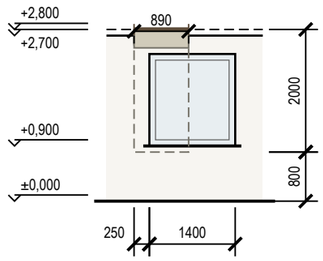


Окно 1 — Кабинет-гостевая (пом. 2): Т7, Т8 (М 1:100)

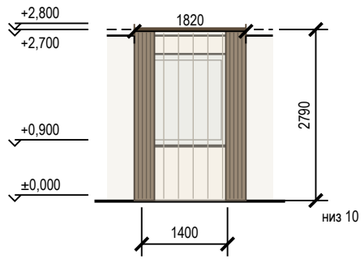


Окно 1 — Гостиная (пом. 5): Т1, Т2 (М 1:100)

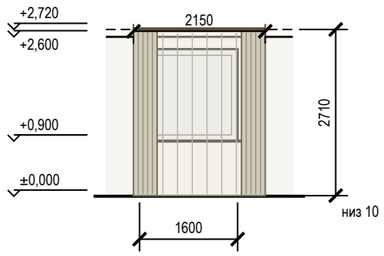


Окно 1 — Спальня мастер (пом. 13): Т13, Т15 (М 1:100)

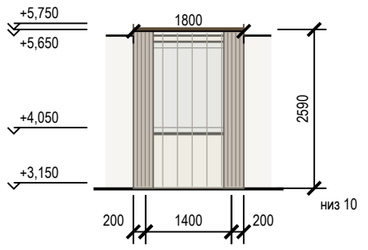


Окно 1 — Спальня 2 (пом. 16): Т20, Т21 (М 1:100)

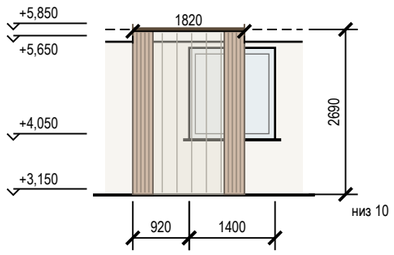

Окно 1 — Спальня 3 (пом. 18): Т26, Т27 (М 1:100)

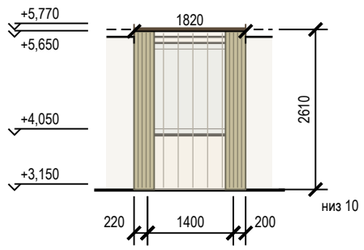

Окно 1 — Спальня 4 (пом. 19): Т32, Т33 (М 1:100)

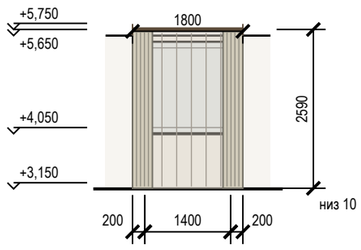

Карта окон: окно → шина → полотно

Поз.	Окно, пом.	Проём Ш×В, подоконник	Верх ниши	Изделие	Шина / карниз: длина, крепление	Верх шины	Полотно: длина, низ	Управление
Т14	1, пом. 1	1400×1500, подок. 900	+2,800	рулонная штора	шина, 890, в нише потолка, вынос 120	+2,800	2000, низ 800	без шнура
Т7	1, пом. 2	1400×1500, подок. 900	+2,800	портьеры	шина, 1820, в нише потолка, вынос 150	+2,800	2790, низ 10 (парит)	вручную
Т8	1, пом. 2	1400×1500, подок. 900	+2,800	тюль	шина, 1820, в нише потолка, вынос 150	+2,800	2790, низ 10 (парит)	вручную
Т1	1, пом. 5	1600×1500, подок. 900	+2,720	портьеры	шина, 2150, в нише потолка, вынос 150	+2,720	2710, низ 10 (парит)	вручную
Т2	1, пом. 5	1600×1500, подок. 900	+2,720	тюль	шина, 2150, в нише потолка, вынос 100	+2,720	2710, низ 10 (парит)	вручную
Т13	1, пом. 13	1400×1500, подок. 900		портьеры	шина, 1800, на потолок, вынос 150	+5,750	2590, низ 10 (парит)	вручную
Т15	1, пом. 13	1400×1500, подок. 900		тюль	шина, 1800, на потолок, вынос 150	+5,750	2590, низ 10 (парит)	вручную
Т20	1, пом. 16	1400×1500, подок. 900	+5,850	портьеры	шина, 1820, в нише потолка, вынос 150	+5,850	2690, низ 10 (парит)	вручную
Т21	1, пом. 16	1400×1500, подок. 900	+5,850	тюль	шина, 1820, в нише потолка, вынос 150	+5,850	2690, низ 10 (парит)	вручную
Т26	1, пом. 18	1400×1500, подок. 900	+5,770	портьеры	шина, 1820, в нише потолка, вынос 150	+5,770	2610, низ 10 (парит)	вручную
Т27	1, пом. 18	1400×1500, подок. 900	+5,770	тюль	шина, 1820, в нише потолка, вынос 150	+5,770	2610, низ 10 (парит)	вручную
Т32	1, пом. 19	1400×1500, подок. 900		портьеры	шина, 1800, на потолок, вынос 150	+5,750	2590, низ 10 (парит)	вручную
Т33	1, пом. 19	1400×1500, подок. 900		тюль	шина, 1800, на потолок, вынос 150	+5,750	2590, низ 10 (парит)	вручную

Условные обозначения

- портьеры в открытом положении
- римская штора: сложена / опущена
- верх ниши под шторы в потолке
- тюль (на виде окна — прозрачная плашка)
- шина или карниз на отметке верха
- оконный проём

Допущения и предложения на листе

Основа листа: размеры и контуры этажей подобраны проектировщиком по составу помещений и площадям этажей с картинки 470 px (размеры на ней не читаются); обмер и исходный проект — задание (К-1); высоты: 1-й этаж 2800 мм, мансарда 2700 мм (горизонтальная часть) приняты; скаты кровли мансарды приняты по картинке: колено 1200 мм, уклон 45°, конёк вдоль длинной стороны; проект КР — задание (К-2); наружные стены 400 мм, перегородки 120 мм приняты (К-1); разрешённая мощность 15 кВт принята по типовым ТУ для частного дома (К-4); подрайон климата не задан — принят не северный (жилые от 2,5 м) (К-7).

Знак «**» — предложение проектировщика, заказчиком не утверждено (согласовать с заказчиком): К-9: дверь пом. 5 (стена В) — проём 2400×2100 на веранду с картинки: одной распашной створкой не закрывается (полотна 600–900) — раздвижная двустворчатая, остеклённая; система и полотна — по каталогу после утверждения автором.

См. лист открытых вопросов (лист 8, записи К-1, К-2, К-4, К-7; лист 9, запись К-9).

Примечания

1. Отметки — в м от ±0,000 (чистый пол 1-го этажа); размеры — мм.
2. Шины в нишах потолка: закладная (брус или профиль) по всей длине ниши — до обшивки ГКЛ; ниша и её отметка — узел ниши на плане потолков (лист 73).
3. Шина в нише — на отметке верха ниши (крепление к закладной в потолке ниши); длина полотна — от верха шины до чистого пола за вычетом зазора.
4. Полотно портьер «парит» над полом на 10 мм; сборка портьер — 2,0, тюля — 2,5 (ширина полотна — в ведомости текстиля).
5. Шнур римской шторы — с натяжителем, петля низом не ниже 1500 мм от пола (защита детей; EN 13120 — рекомендация).
6. Электрокарнизы не предусмотрены; при замене на электропривод — вывод кабеля в нише у края шины (задание электрику).
7. Марки изделий — по плану текстиля и декора (лист 100) и ведомости текстиля (лист 103).

Изм.	Кол.уч	Лист	№ док.	Подп.	Дата
Разраб.		Кырлан А.С.			04.11.26
Пров.					
ГИП					
Н. контр.					
Утв.					

ГД-2026-010-АИ

Дом 331 м²

Общая площадь 270,67* м² · * размеры приняты, не замерены (реестр — л. 8–10, К-1)

Дизайн-проект интерьера

Стадия	Лист	Листов
РП	102	216

Шторы и карнизы

М б/м

Кырлан Александр Сергеевич

выпуск 04.11.2026 № 2a77323a49 · стр. 105 из 221

Ведомость текстиля

Шторы, тюль, римские шторы, ковры, подушки и пледы · размеры в мм · марки — по плану текстиля и декора

Текстиль: шторы, ковры, подушки, пледы

Поз.	Пом.	Изделие	Размер, мм	Ткань, состав, плотность	Сборка, ширина полотна		Цвет (система, код)	Кол.	Примечание
T1	5	Портьеры-волна, два полотна	шина 2150 × полотно 2710	лён 100 %; 280 г/м²	× 2, ширина 4300		NCS S 2005-Y20R (Светлый песочно-серый)	2	низ 10 (парит); в нише потолка; уход: химчистка; отпаривание на карнизе
T2	5	Тюль-вуаль, одно полотно	шина 2150 × полотно 2710	вуаль; полиэстер 100 %; 60 г/м²	× 2,5, ширина 5375		NCS S 0804-Y30R (тёплый молочный белый)	1	низ 10 (парит); в нише потолка; уход: стирка 30 °C, вешать влажной
T3	5	Ковёр мягкой группы, шерсть с джутом	3600×2400	шерсть с джутом, рельефное плетение; шерсть 100 %			Farrow & Ball No. 243 (Charleston Gray серо-коричневый «камень»)	1	противоскользящая подложка; ворс 12 мм; уход: сухая чистка, пылесос без турбощётки
T4	5	Подушки декоративные на диван, лён	500×500	лён 100 %			Farrow & Ball No. 226 (Joa's White)	3	на Гс2; уход: съёмный чехол, стирка 30 °C
T5	5	Подушки декоративные на диван, акцент	400×600	хлопковый бархат 100 %			Farrow & Ball No. 93 (Studio Green — почти чёрный зелёный)	2	на Гс2; уход: химчистка
T6	5	Плед на диван	1300×1700	шерсть мериноса 100 %			Farrow & Ball No. 93 (Studio Green — почти чёрный зелёный)	1	на Гс2; уход: ручная стирка 30 °C
T7	2	Портьеры на люверсах, шерстяной твид	шина 1820 × полотно 2790	шерстяной твид с подкладкой; лён 100 %; 320 г/м²; блэкаут	× 2, ширина 3640		Farrow & Ball No. 40 (Mouse's Back — тёплый коричнево-серый)	2	низ 10 (парит); в нише потолка
T8	2	Тюль, льняная сетка	шина 1820 × полотно 2790	лён-сетка; полиэстер 100 %	× 2,5, ширина 4550		NCS S 0804-Y30R (тёплый молочный белый)	1	низ 10 (парит); в нише потолка
T9	2	Ковёр джутовый под диваном	1700×2300	джут плетёный; шерсть 100 %			Tikkurila X463 (бежевый песчаник)	1	противоскользящая подложка; ворс 6 мм
T10	2	Подушки на диван, кожа	500×500	кожа натуральная, коньяк; букле (шерсть 60 %, полиэстер 40 %)			NCS S 3010-Y30R (орех/лён тёмный)	3	на Кб3
T11	2	Подушки на кровать, акцент	400×600	хлопковый бархат 100 %			Farrow & Ball No. 298 (Bancha)	2	на Кб3
T12	2	Плед на кровать	1300×1700	шерсть мериноса 100 %			Farrow & Ball No. 298 (Bancha)	1	на Кб3
T13	13	Портьеры-волна, шерсть с блэкаут-подкладкой	шина 1800 × полотно 2590	шерсть плотная с блэкаут-подкладкой; лён 100 %; 320 г/м²	× 2, ширина 5000		Farrow & Ball No. 229 (Elephant's Breath тёплый средне-серый с лиловым подтоном)	2	низ 10 (парит); на потолок
T14	1	Рулонная штора кассетная, ткань димаут	шина 890 × полотно 2000	ткань димаут с грязеотталкивающей пропиткой; полиэстер 100 %			NCS S 2005-Y20R (Светлый песочно-серый)	1	низ 800; в нише потолка; шнур: петля —, cordless; уход: протирка влажной губкой
T15	13	Тюль	шина 1800 × полотно 2590	вуаль; полиэстер 100 %	× 2,5, ширина 6250		Little Greene No. 105 (Slaked Lime)	1	низ 10 (парит); на потолок
T16	13	Ковёр под кроватью, шерсть ручного ткачества	2800×1900	шерсть, ручное ткачество; шерсть 80 %, хлопок 20 %			NCS S 2005-Y20R (Светлый песочно-серый)	1	противоскользящая подложка; ворс 10 мм
T17	13	Подушки декоративные на кровать, шерсть-меланж	500×500	шерсть-меланж; лён 100 %			NCS S 2005-Y20R (Светлый песочно-серый)	3	на М1
T18	13	Подушки на кровать, акцент	400×600	хлопковый бархат 100 %			NCS S 7020-G10Y (Хвойный тёмно-зелёный)	2	на М1
T19	13	Плед на кровать	1300×1700	шерсть мериноса 100 %			NCS S 7020-G10Y (Хвойный тёмно-зелёный)	1	на М1
T20	16	Портьеры-волна, хлопок-сатин с блэкаут-подкладкой	шина 1820 × полотно 2690	хлопок-сатин с блэкаут-подкладкой; лён 100 %; 320 г/м²	× 2, ширина 3640		Tikkurila X463 (бежевый песчаник)	2	низ 10 (парит); в нише потолка
T21	16	Тюль, лён-вуаль	шина 1820 × полотно 2690	лён-вуаль; полиэстер 100 %	× 2,5, ширина 4550		Little Greene No. 105 (Slaked Lime)	1	низ 10 (парит); в нише потолка
T22	16	Ковёр под кроватью, шерсть с узором ромбы	2000×2500	шерсть, ворсовый, узор ромбы; шерсть 100 %			NCS S 3010-Y30R (орех/лён тёмный)	1	противоскользящая подложка; ворс 15 мм
T23	16	Подушки декоративные на кровать, хлопок-рогожка	500×500	хлопок-рогожка; букле (шерсть 60 %, полиэстер 40 %)			Tikkurila X463 (бежевый песчаник)	3	на С1
T24	16	Подушки на кровать, акцент	400×600	хлопковый бархат 100 %			Farrow & Ball No. 64 (Red Earth)	2	на С1
T25	16	Плед на кровать	1300×1700	шерсть мериноса 100 %			Farrow & Ball No. 64 (Red Earth)	1	на С1

Продолжение ведомости — на следующем листе; итог и примечания — на последнем листе ведомости.

Допущения и предложения на листе

Основа листа: размеры и контуры этажей подобраны проектировщиком по составу помещений и площадям этажей с картинки 470 px (размеры на ней не читаются); обмер и исходный проект — задание (К-1); высоты: 1-й этаж 2800 мм, мансарда 2700 мм (горизонтальная часть) приняты; скаты кровли мансарды приняты по картинке: колено 1200 мм, уклон 45°, конёк вдоль длинной стороны; проект КР — задание (К-2); наружные стены 400 мм, перегородки 120 мм приняты (К-1); разрешённая мощность 15 кВт принята по типовым ТУ для частного дома (К-4); подрайон климата не задан — принят не северный (жилые от 2,5 м) (К-7).

См. лист открытых вопросов (лист 8, записи К-1, К-2, К-4, К-7).

Изм.	Кол.уч	Лист	№ док.	Подп.	Дата
Разраб.		Кырлан А.С.			04.11.26
Пров.					
ГИП					
Н. контр.					
Утв.					

ГД-2026-010-АИ

Дом 331 м²

Общая площадь 270,67* м² · * размеры приняты, не замерены (реестр — л. 8–10, К-1)

Дизайн-проект интерьера

Стадия	Лист	Листов
РП	103	216

Ведомость текстиля

М б/м

Кырлан Александр Сергеевич

выпуск 04.11.2026 № 2a77323a49 · стр. 106 из 221

Ведомость текстиля (продолжение)

Шторы, тюль, римские шторы, ковры, подушки и пледы · размеры в мм · марки — по плану текстиля и декора

Текстиль: шторы, ковры, подушки, пледы (продолжение)

Поз.	Пом.	Изделие	Размер, мм	Ткань, состав, плотность	Сборка, ширина полотна		Цвет (система, код)	Кол.	Примечание
T26	18	Портьеры на люверсах, хлопок-канвас с блэкаут-подкладкой	шина 1820 × полотно 2610	хлопок-канвас с блэкаут-подкладкой; лён 100 %; 320 г/м²	× 2, ширина 3640		Tikkurila V451 (выцветший оливковый)	2	низ 10 (парит); в нише потолка
T27	18	Тюль, хлопковая кисея	шина 1820 × полотно 2610	хлопковая кисея; полиэстер 100 %	× 2,5, ширина 4550		NCS S 0804-Y30R (тёплый молочный белый)	1	низ 10 (парит); в нише потолка
T28	18	Ковёр под кроватью, хлопок, стираемый	1600×1200	хлопок, плоское плетение, стираемый; шерсть 100 %			NCS S 2005-Y20R (Светлый песочно-серый)	1	противоскользящая подложка; ворс 5 мм
T29	18	Подушки на кровать, хлопок-вельвет	500×500	хлопок-вельвет; букле (шерсть 60 %, полиэстер 40 %)			Tikkurila V451 (выцветший оливковый)	3	на Дт1
T30	18	Подушки на кровать, акцент	400×600	хлопковый бархат 100 %			NCS S 3020-G30Y (шалфей)	2	на Дт1
T31	18	Плед на кровать	1300×1700	шерсть мериноса 100 %			NCS S 3020-G30Y (шалфей)	1	на Дт1
T32	19	Портьеры-волна, лён-меланж с блэкаут-подкладкой	шина 1800 × полотно 2590	лён-меланж с блэкаут-подкладкой; лён 100 %; 320 г/м²	× 2, ширина 3640		NCS S 2005-Y20R (Светлый песочно-серый)	2	низ 10 (парит); на потолок
T33	19	Тюль, лён-вуаль в мелкую клетку	шина 1800 × полотно 2590	лён-вуаль; полиэстер 100 %	× 2,5, ширина 4550		Farrow & Ball No. 226 (Joa's White)	1	низ 10 (парит); на потолок
T34	19	Ковёр под кроватью, шерсть с узором «горы»	1600×1200	шерсть, ворсовый, тафтинг; шерсть 100 %			NCS S 3010-Y30R (орех/лён тёмный)	1	противоскользящая подложка; ворс 12 мм
T35	19	Подушки на кровать, хлопок-канвас с принтом	500×500	хлопок-канвас с принтом; букле (шерсть 60 %, полиэстер 40 %)			Tikkurila X463 (бежевый песчаник)	3	на Дт4
T36	19	Подушки на кровать, акцент	400×600	хлопковый бархат 100 %			NCS S 3040-Y70R (обожжённая глина)	2	на Дт4
T37	19	Плед на кровать	1300×1700	шерсть мериноса 100 %			NCS S 3040-Y70R (обожжённая глина)	1	на Дт4
T40	10	Покрытие резиновое модульное 500×500×10 мм под спортзону	1500×6300	резиновая крошка SBR с цветными EPDM-вкраплениями, плиты 500×500, 10 мм			Farrow & Ball No. 243 (Charleston Gray серо-коричневый «камень»)	1	
T41	17	Коврик для йоги и растяжки 1830×610×6, TPE, нескользящий	610×1830	TPE, 6 мм, двухслойный			NCS S 3020-G30Y (шалфей)	1	

образец цвета — по HEX производителя краски, справочно

Итого: шторы и тюль — 19 шт.; ковры и дорожки — 8 шт.; подушки, пледы, покрывала — 36 шт.


Образцы по помещениям

1. Кухня-столовая




T14

2. Кабинет-гостевая

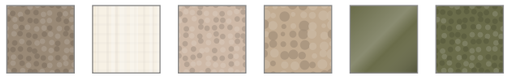

T7 T8 T9 T10 T11 T12

5. Гостиная

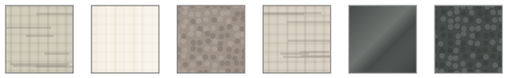


T1 T2 T3 T4 T5 T6

10. Гараж



T40

13. Спальня мастер

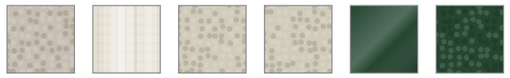

T13 T15 T16 T17 T18 T19

Примечания

1. Коды цвета — ориентир подбора по веерам производителей красок; ткань утверждается по образцу при дневном свете и при свете проекта 2700–3000 K.
2. Размеры полотен — по замеру после чистовой отделки пола и потолка; ширина полотна указана с учётом сборки, без припусков на швы. Схемы окон и отметки шин лист 102.
3. Портьеры и тюль — на тесьме «волна» по системе шины; блэкаут — подкладкой. Ковры — на противоскользящей подложке.
4. Замена изделия — аналогом по характеристикам (состав, плотность, размер, цвет по образцу) с согласованием автора проекта.
5. Места изделий — план текстиля и декора (лист 100); подушки и пледы — по марке мебели.

Допущения и предложения на листе

Основа листа: размеры и контуры этажей подобраны проектировщиком по составу помещений и площадям этажей с картинки 470 px (размеры на ней не читаются); обмер и исходный проект — задание (К-1); высоты: 1-й этаж 2800 мм, мансарда 2700 мм (горизонтальная часть) приняты; скаты кровли мансарды приняты по картинке: колено 1200 мм, уклон 45°, конёк вдоль длинной стороны; проект КР — задание (К-2); наружные стены 400 мм, перегородки 120 мм приняты (К-1); разрешённая мощность 15 кВт принята по типовым ТУ для частного дома (К-4); подрайон климата не задан — принят не северный (жилые от 2,5 м) (К-7).

См. лист открытых вопросов (лист 8, записи К-1, К-2, К-4, К-7).

Изм.	Кол.уч	Лист	№ док.	Подп.	Дата
Разраб.		Кырлан А.С.			04.11.26
Пров.					
ГИП					
Н. контр.					
Утв.					

ГД-2026-010-АИ

Дом 331 м²

Общая площадь 270,67* м² · * размеры приняты, не замерены (реестр — л. 8–10, К-1)

Дизайн-проект интерьера

Стадия	Лист	Листов
РП	104	216

Ведомость текстиля (продолжение)

М б/м

Кырлан Александр Сергеевич

выпуск 04.11.2026 № 2a77323a49 · стр. 107 из 221

Ведомость декора

Картины, зеркала, растения, настольный декор · высоты — мм от чистого пола

Декор: картины, зеркала, растения, предметы

Поз.	Пом.	Предмет	Размер, мм	Место: стена, высота от пола, мм	Масса, кг	Крепёж и основание	Свет места, отделка	Кол.
ДК1	5	Картина над буфетом: Еловый лес в тумане над горным озером, масло	1200×900	стена Б, привязка 2740; низ 1000, центр 1450; над Гс6	6	планка на дюбелях, 4 точки; основание: перегородка 120 мм; нагрузка 20 кг		1
ДК2	5	Фикус лировидный в кашпо Ø400	450×450	напольное			свет яркий рассеянный	1
ДК3	2	Картина над диваном: Старинная карта горного хребта, офорт в паспарту	1000×700	стена Г, привязка 1700; низ 1100, центр 1450; над К63	4	подвес по основанию, 2 точки	рама — дуб	1
ДК4	13	Картина над кроватью: Ветви лиственницы с шишками, акварель	1000×700	стена А, привязка 3600; низ 1300, центр 1650; над М1	4	подвес по основанию, 2 точки	рама — дуб	1
ДК5	8	Зеркало	800×1800	стена Б, привязка 540; низ 550, центр 1450	18	анкер, 4 шт.; основание: перегородка — определить обмером до монтажа; нагрузка 40 кг	рама — чёрный матовый металл	1
ДК6	16	Картина над кроватью: Глиняный кувшин с полевыми цветами, масло	1000×700	стена Б, привязка 3040; низ 1300, центр 1650; над С1	4	подвес по основанию, 2 точки	рама — дуб	1
ДК7	16	Зеркало в рост в раме из ясеня	600×1600	стена Г, привязка 1440; низ 300, центр 1100	12	анкер для пустотелых оснований, 4 шт.; основание: перегородка — определить обмером до монтажа; нагрузка 30 кг	рама — чёрный матовый металл	1
ДК8	1	Часы настенные Ø400	400×400	стена В, привязка 1200; центр 1550	2	дюбель с крюком, 1 точка; основание: перегородка 120 мм; нагрузка 10 кг		1
ДК9	1	Хлорофитум хохлатый на подоконнике (отм. +0,800)	300×200	напольное			свет средний	1
ДК10	18	Картина над кроватью: Рыжая лиса под ёлкой, детская иллюстрация	600×700	стена А, привязка 150; низ 1100, центр 1450; над Дт1	4	подвес по основанию, 2 точки	рама — дуб	1
ДК11	18	Зеркало безопасное (плёнка), рама — светлый ясень	500×1600	стена Г, привязка 2340; низ 300, центр 1100	12	анкер для пустотелых оснований, 4 шт.; основание: перегородка — определить обмером до монтажа; нагрузка 30 кг	рама — чёрный матовый металл	1
ДК12	19	Картина над кроватью: Горы из цветных треугольников, детский принт	600×700	стена А, привязка 150; низ 1100, центр 1450; над Дт4	4	подвес по основанию, 2 точки	рама — дуб	1
ДК13	19	Зеркало круглое Ø600 в кожаном ремне	600×600	стена Г, привязка 2140; низ 1150, центр 1450	12	анкер для пустотелых оснований, 4 шт.; основание: перегородка — определить обмером до монтажа; нагрузка 30 кг	рама — чёрный матовый металл	1
ДК21	5	Оливковое дерево в кашпо Ø450	450×450	напольное			свет яркий рассеянный	1
ДК22	5	Ваза с живыми цветами на журнальном столе	200×350	на Гс3				1
ДК23	1	Ваза с тюльпанами на обеденном столе	200×350	на Кх8 (обеденный стол)				1
ДК24	11	Гортензия крупнолистная в кадке Ø500	500×500	напольное			свет средний	1
ДК25	11	Самшит в кадке Ø450	450×450	напольное			свет средний	1
ДК26	11	Папоротник нефролепис в ящике 600×250	250×600	напольное			свет средний	1
ДК27	13	Фикус каучуконосный в кашпо Ø400	400×400	напольное			свет средний	1
ДК28	2	Замиокулькас в кашпо Ø350	350×350	напольное			свет слабый	1
ДК30	17	Монстера в кашпо Ø450 с фитолампой	450×450	напольное			свет средний, фитолампа	1
ДК31	10	Зеркало 1200×1500 для контроля техники, безопасное (плёнка), без рамы	1200×1500	стена Б, привязка 4000; низ 600, центр 1350	22	анкер, 4 шт.; основание: наружная стена 400 мм — материал определить обмером до монтажа; нагрузка 50 кг		1

Допущения и предложения на листе

Основа листа: размеры и контуры этажей подобраны проектировщиком по составу помещений и площадям этажей с картинки 470 px (размеры на ней не читаются); обмер и исходный проект — задание (К-1); высоты: 1-й этаж 2800 мм, мансарда 2700 мм (горизонтальная часть) приняты; скаты кровли мансарды приняты по картинке: колено 1200 мм, уклон 45°, конёк вдоль длинной стороны; проект КР — задание (К-2); наружные стены 400 мм, перегородки 120 мм приняты (К-1); разрешённая мощность 15 кВт принята по типовым ТУ для частного дома (К-4); подрайон климата не задан — принят не северный (жилые от 2,5 м) (К-7).

См. лист открытых вопросов (лист 8, записи К-1, К-2, К-4, К-7).

Примечания

1. Высоты — от чистого пола помещения до низа изделия, «ц» — до центра; привязки — от чистовой грани угла стены, мм.
2. Над мебелью низ изделия — на 150–250 мм выше спинки или изголовья; без мебели центр — на 1450–1600 мм от пола.
3. Изделия до 5 кг — на два подвеса по основанию; тяжелее — на анкеры с нагрузкой не меньше двойной массы; на ГКЛ — только по закладной или анкеру для пустотелых оснований.
4. Зеркала в рост — с креплением от опрокидывания; в санузлах — влагостойкие, на клей для зеркал и нейтральный силикон.
5. Места изделий — план текстиля и декора (лист 100). Схемы развески — лист 106, 107.

Изм.	Кол.уч	Лист	№ док.	Подп.	Дата
Разраб.		Кырлан А.С.			04.11.26
Пров.					
ГИП					
Н. контр.					
Утв.					

ГД-2026-010-АИ

Дом 331 м²

Общая площадь 270,67* м² · * размеры приняты, не замерены (реестр — л. 8–10, К-1)

Дизайн-проект интерьера

Стадия	Лист	Листов
РП	105	216

Ведомость декора

М б/м

Кырлан Александр Сергеевич

выпуск 04.11.2026 № 2a77323a49 · стр. 108 из 221


Схемы развески

Схемы развески картин и зеркал (М 1:50) · высоты — мм от чистого пола


Ведомость декора (размер, масса, крепёж и основание) — лист 105

картина · зеркало · мебель под изделием


ДК1 — Гостиная (пом. 5), стена Б (М 1:50)

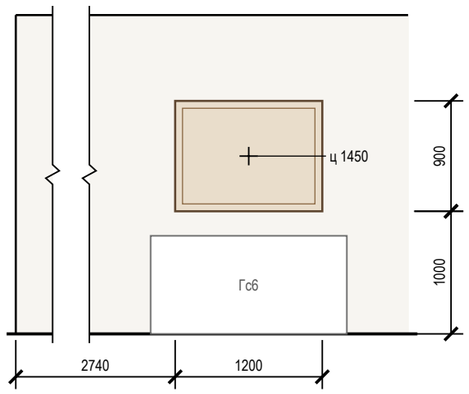


ДК3 — Кабинет-гостевая (пом. 2), стена Г (М 1:50)

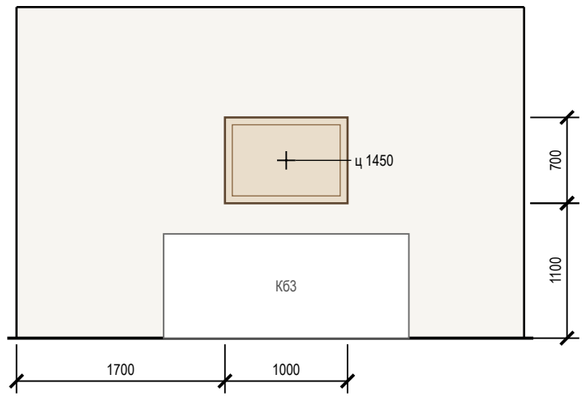


ДК4 — Спальня мастер (пом. 13), стена А (М 1:50)

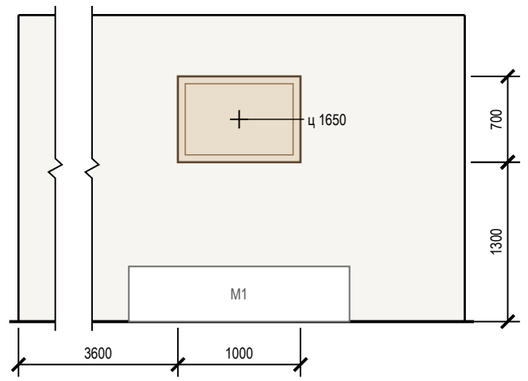


ДК5 — Прихожая (пом. 8), стена Б (М 1:50)

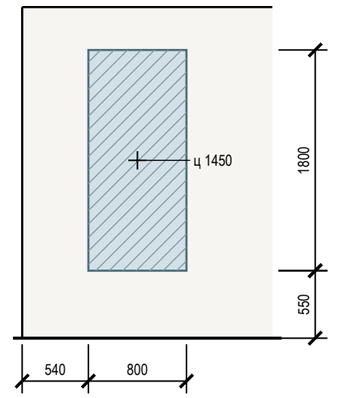

ДК6 — Спальня 2 (пом. 16), стена Б (М 1:50)

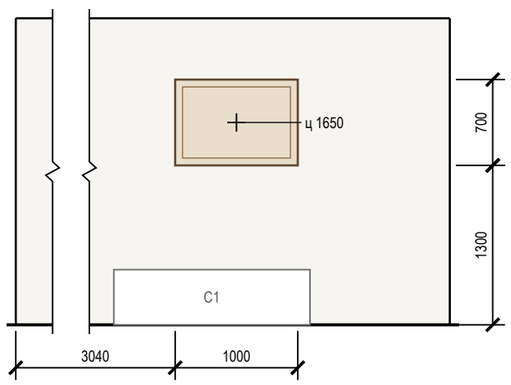

ДК7 — Спальня 2 (пом. 16), стена Г (М 1:50)

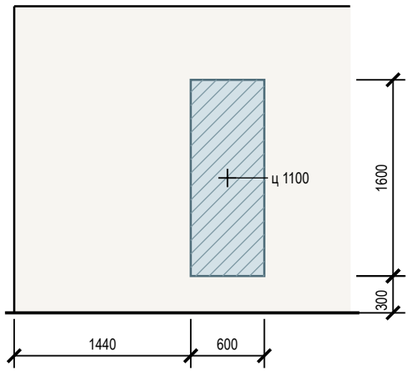

Допущения и предложения на листе

Основа листа: размеры и контуры этажей подобраны проектировщиком по составу помещений и площадям этажей с картинки 470 px (размеры на ней не читаются); обмер и исходный проект — задание (К-1); высоты: 1-й этаж 2800 мм, мансарда 2700 мм (горизонтальная часть) приняты; скаты кровли мансарды приняты по картинке: колено 1200 мм, уклон 45°, конёк вдоль длинной стороны; проект КР — задание (К-2); наружные стены 400 мм, перегородки 120 мм приняты (К-1); разрешённая мощность 15 кВт принята по типовым ТУ для частного дома (К-4); подрайон климата не задан — принят не северный (жилые от 2,5 м) (К-7).

См. лист открытых вопросов (лист 8, записи К-1, К-2, К-4, К-7).

Примечания

1. Высоты — от чистого пола помещения до низа изделия, «ц» — до центра; привязки — от чистовой грани угла стены, мм.
2. Над мебелью низ изделия — на 150–250 мм выше спинки или изголовья; без мебели центр — на 1450–1600 мм от пола.
3. Изделия до 5 кг — на два подвеса по основанию; тяжелее — на анкеры с нагрузкой не меньше двойной массы; на ГКЛ — только по закладной или анкеру для пустотелых оснований.
4. Зеркала в рост — с креплением от опрокидывания; в санузлах — влагостойкие, на клей для зеркал и нейтральный силикон.
5. Места изделий — план текстиля и декора (лист 100). Схемы развески остальных изделий — лист 107. Ведомость декора: размер, масса, крепёж и основание лист 105.

Изм.	Кол.уч	Лист	№ док.	Подп.	Дата
Разраб.		Кырлан А.С.			04.11.26
Пров.					
ГИП					
Н. контр.					
Утв.					

ГД-2026-010-АИ

Дом 331 м²

Общая площадь 270,67* м² · * размеры приняты, не замерены (реестр — л. 8–10, К-1)

Дизайн-проект интерьера

Стадия	Лист	Листов
РП	106	216

Схемы развески

М б/м

Кырлан Александр Сергеевич

выпуск 04.11.2026 № 2a77323a49 · стр. 109 из 221


Схемы развески (продолжение)

Схемы развески картин и зеркал (М 1:50) · высоты — мм от чистого пола


Ведомость декора (размер, масса, крепёж и основание) — лист 105

картина · зеркало · мебель под изделием


ДК8 — Кухня-столовая (пом. 1), стена В (М 1:50)

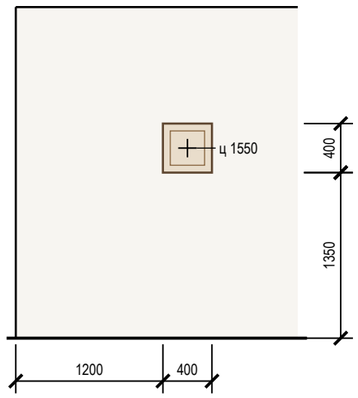


ДК10 — Спальня 3 (пом. 18), стена А (М 1:50)

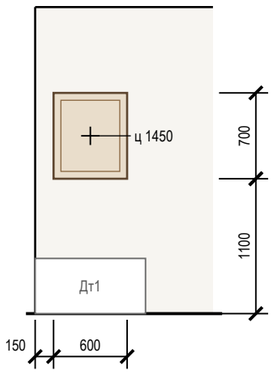


ДК11 — Спальня 3 (пом. 18), стена Г (М 1:50)

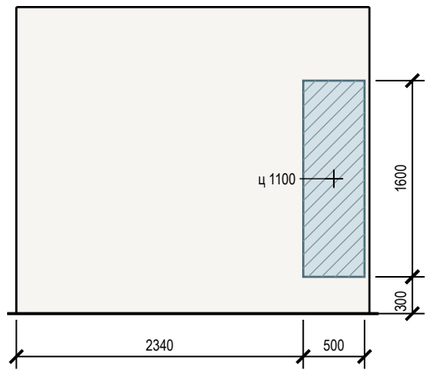


ДК12 — Спальня 4 (пом. 19), стена А (М 1:50)

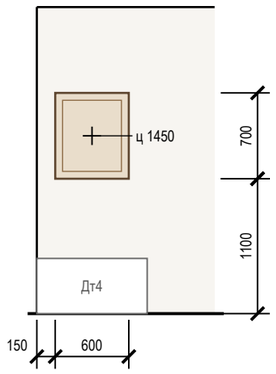

ДК13 — Спальня 4 (пом. 19), стена Г (М 1:50)

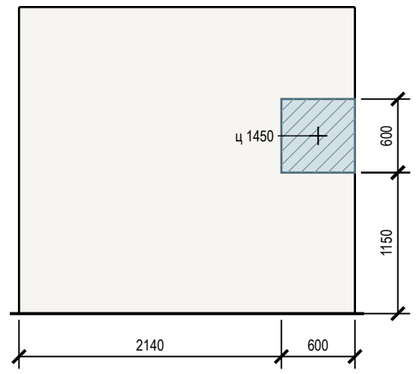

ДК31 — Гараж (пом. 10), стена Б (М 1:50)

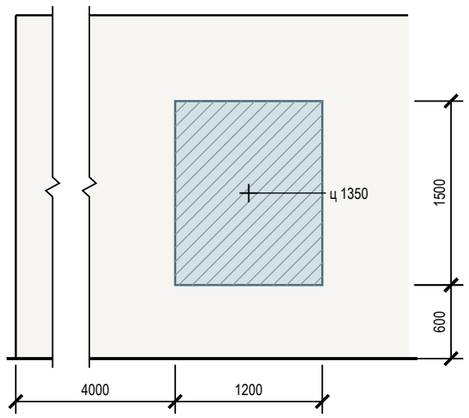

Допущения и предложения на листе

Основа листа: размеры и контуры этажей подобраны проектировщиком по составу помещений и площадям этажей с картинки 470 px (размеры на ней не читаются); обмер и исходный проект — задание (К-1); высоты: 1-й этаж 2800 мм, мансарда 2700 мм (горизонтальная часть) приняты; скаты кровли мансарды приняты по картинке: колено 1200 мм, уклон 45°, конёк вдоль длинной стороны; проект КР — задание (К-2); наружные стены 400 мм, перегородки 120 мм приняты (К-1); разрешённая мощность 15 кВт принята по типовым ТУ для частного дома (К-4); подрайон климата не задан — принят не северный (жилые от 2,5 м) (К-7).

См. лист открытых вопросов (лист 8, записи К-1, К-2, К-4, К-7).

Примечания

1. Высоты — от чистого пола помещения до низа изделия, «ц» — до центра; привязки — от чистовой грани угла стены, мм.
2. Над мебелью низ изделия — на 150–250 мм выше спинки или изголовья; без мебели центр — на 1450–1600 мм от пола.
3. Изделия до 5 кг — на два подвеса по основанию; тяжелее — на анкеры с нагрузкой не меньше двойной массы; на ГКЛ — только по закладной или анкеру для пустотелых оснований.
4. Зеркала в рост — с креплением от опрокидывания; в санузлах — влагостойкие, на клей для зеркал и нейтральный силикон.
5. Места изделий — план текстиля и декора (лист 100). Схемы развески остальных изделий — лист 106. Ведомость декора: размер, масса, крепёж и основание лист 105.

Изм.	Кол.уч	Лист	№ док.	Подп.	Дата
Разраб.		Кырлан А.С.			04.11.26
Пров.					
ГИП					
Н. контр.					
Утв.					

ГД-2026-010-АИ

Дом 331 м²

Общая площадь 270,67* м² · * размеры приняты, не замерены (реестр — л. 8–10, К-1)

Дизайн-проект интерьера

Стадия	Лист	Листов
РП	107	216

Схемы развески (продолжение)

М б/м


Кырлан Александр Сергеевич

выпуск 04.11.2026 № 2a77323a49 · стр. 110 из 221

Встроенная мебель. Схема расположения · 1-й этаж

встроенная и корпусная мебель на заказ, кухонный гарнитур · размеры в мм · марки — по ведомости изделий

ПРЕДВАРИТЕЛЬНО · не для производства работ · открыто пунктов: 15 (реестр — л. 8–10)

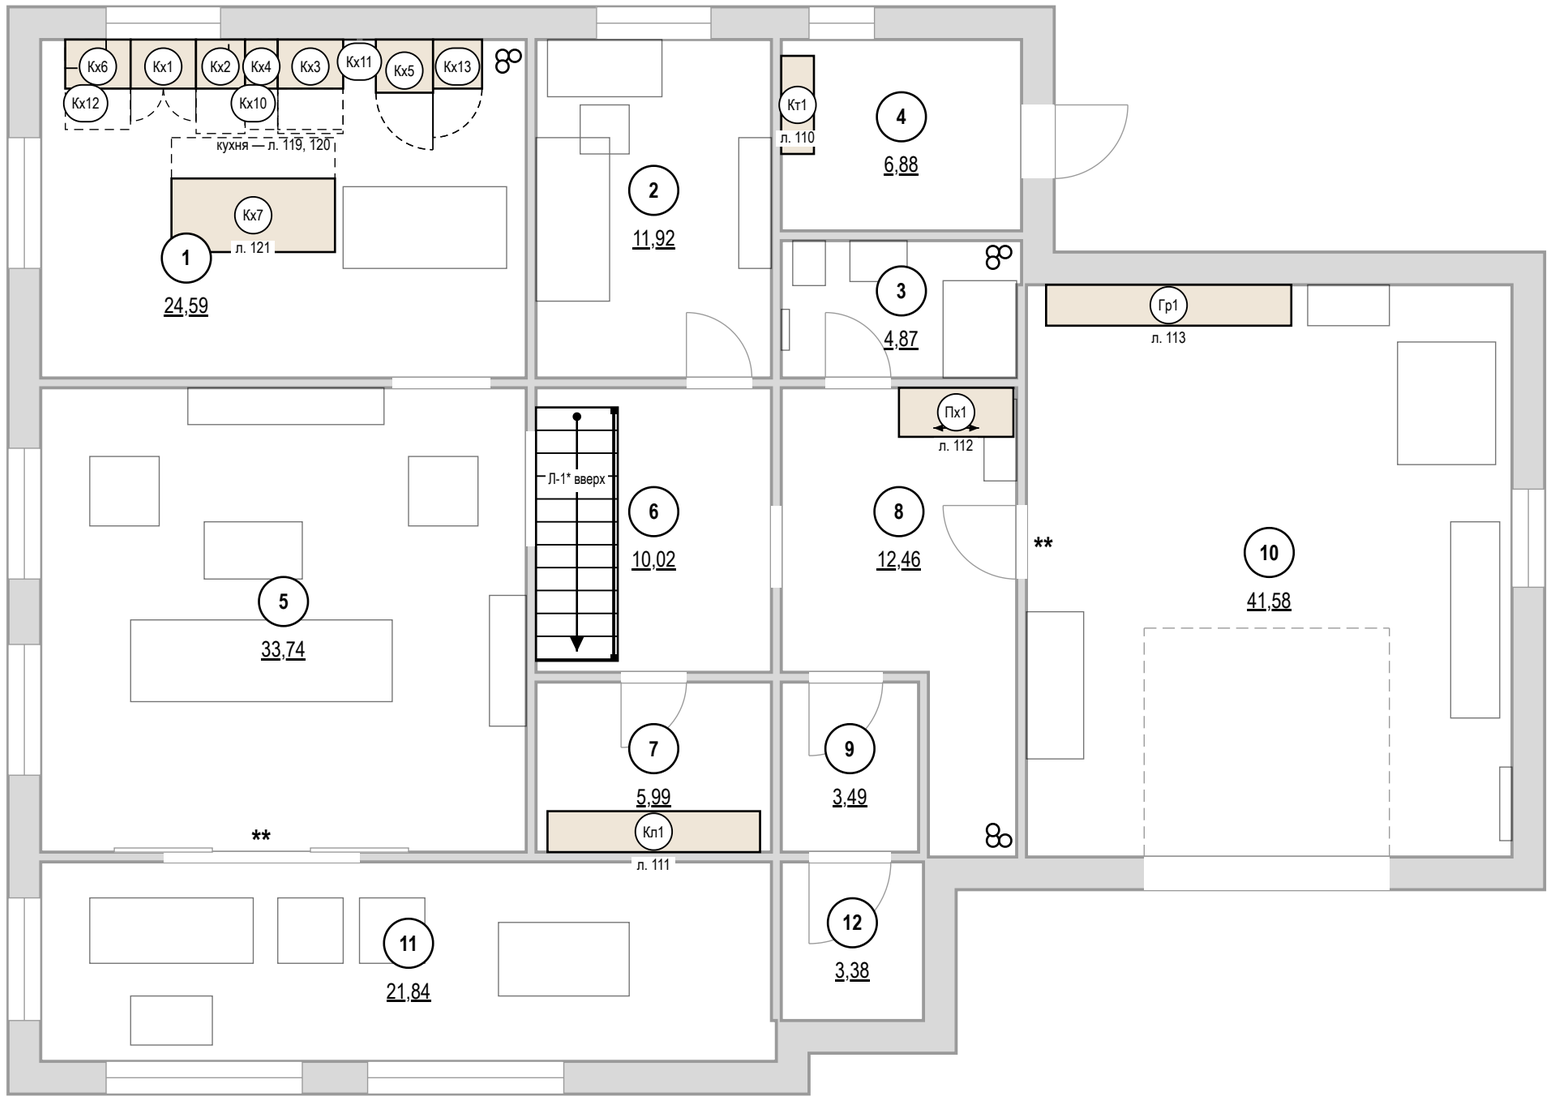

Ведомость изделий

Марка	Наименование	Пом.	Ш×Г×В, мм	Лист
Кт1	Система хранения	4	1200×400×2000	110
Кл1	Система хранения	7	2600×500×2200	111
Пх1	Шкаф-купе	8	1400×600×2600	112
Гр1	Система хранения	10	3000×500×2000	113
Кх6	Модуль нижний: ящики	1	800×600×900	119
Кх12	Модуль навесной: полки	1	500×350×900	119
Кх1	Модуль нижний: мойка	1	800×600×900	119
Кх2	Модуль под ПММ 60: без корпуса, фасад на дверь машины	1	600×600×900	119
Кх10	Модуль навесной: полки	1	600×350×900	119
Кх4	Модуль нижний: ящики	1	400×600×900	119
Кх3	Модуль нижний: духовой шкаф, варочная	1	800×600×900	119
Кх11	Модуль навесной: полки	1	400×350×900	119
Кх5	Пенал: холодильник встр.	1	700×650×2200	119
Кх13	Пенал: полки	1	600×600×2200	119
Кх7	Остров	1	2000×900×900	121

Условные обозначения

- изделие мебельщика: корпус на полу
- невидимый контур: навесной модуль, корпус под столешницей
- открывание распашного фасада
- зона выдвижения ящика, двери техники
- дверь купе, стрелка — направление движения
- К1 — марка изделия или модуля (на схеме расположения под ней — лист изделия)
- ** — «**» — предложение проектировщика, заказчиком не утверждено

Примечания

1. Изделия — по чистовым размерам помещений; перед раскроем — контрольный замер цеха после чистовой отделки стен, пола и потолка.
2. Открывание фасадов и выдвижение ящиков показано в открытом положении: зоны не пересекают двери, радиаторы, выключатели и проходы.
3. Стояки и счётчики за мебелью — с сервисным люком; газовые трубы мебелью не зашиваются.
4. Покупная мебель — по плану расстановки мебели и спецификации дизайнера; здесь — подложкой.

Допущения и предложения на листе. Основа листа: размеры и контуры этажей подобраны проектировщиком по составу помещений и площадям этажей с картинки 470 px (размеры на ней не читаются); обмер и исходный проект — задание (К-1); высоты: 1-й этаж 2800 мм, мансарда 2700 мм (горизонтальная часть) приняты; скаты кровли мансарды приняты по картинке: колено 1200 мм, уклон 45°, конёк вдоль длинной стороны; проект КР — задание (К-2); наружные стены 400 мм, перегородки 120 мм приняты (К-1); разрешённая мощность 15 кВт принята по типовым ТУ для частного дома (К-4); подрайон климата не задан — принят не северный (жилые от 2,5 м) (К-7). Знак «*» — принято, не замерено и не подтверждено (замерить на объекте): К-6: Л-1 — габарит марша снят с картинки заказчика (11 проступей в холле 3,6 м), а до отм. +3,150 нужно 18 подъёмов — одномаршевая не встаёт: решение по К-6. Знак «**» — предложение проектировщика, заказчиком не утверждено (согласовать с заказчиком). См. лист открытых вопросов (лист 8, записи К-1, К-2, К-4, К-6, К-7; лист 9, запись К-9).

1000 мм · печать 1:1

Изм.	Кол.уч	Лист	№ док.	Подп.	Дата
Разраб.		Кырлан А.С.			04.11.26
Пров.					
ГИП					
Н. контр.					
Утв.					

ГД-2026-010-АИ

Дом 331 м²

Общая площадь 270,67* м² · * размеры приняты, не замерены (реестр — л. 8–10, К-1)

Дизайн-проект интерьера	Стадия	Лист	Листов
	РП	108	216

Встроенная мебель. Схема расположения · 1-й этаж

М 1:75


Кырлан Александр Сергеевич

выпуск 04.11.2026 № 2a77323a49 · стр. 111 из 221

Встроенная мебель. Схема расположения · Мансарда

встроенная и корпусная мебель на заказ, кухонный гарнитур · размеры в мм · марки — по ведомости изделий

ПРЕДВАРИТЕЛЬНО · не для производства работ · открыто пунктов: 15 (реестр — л. 8–10)

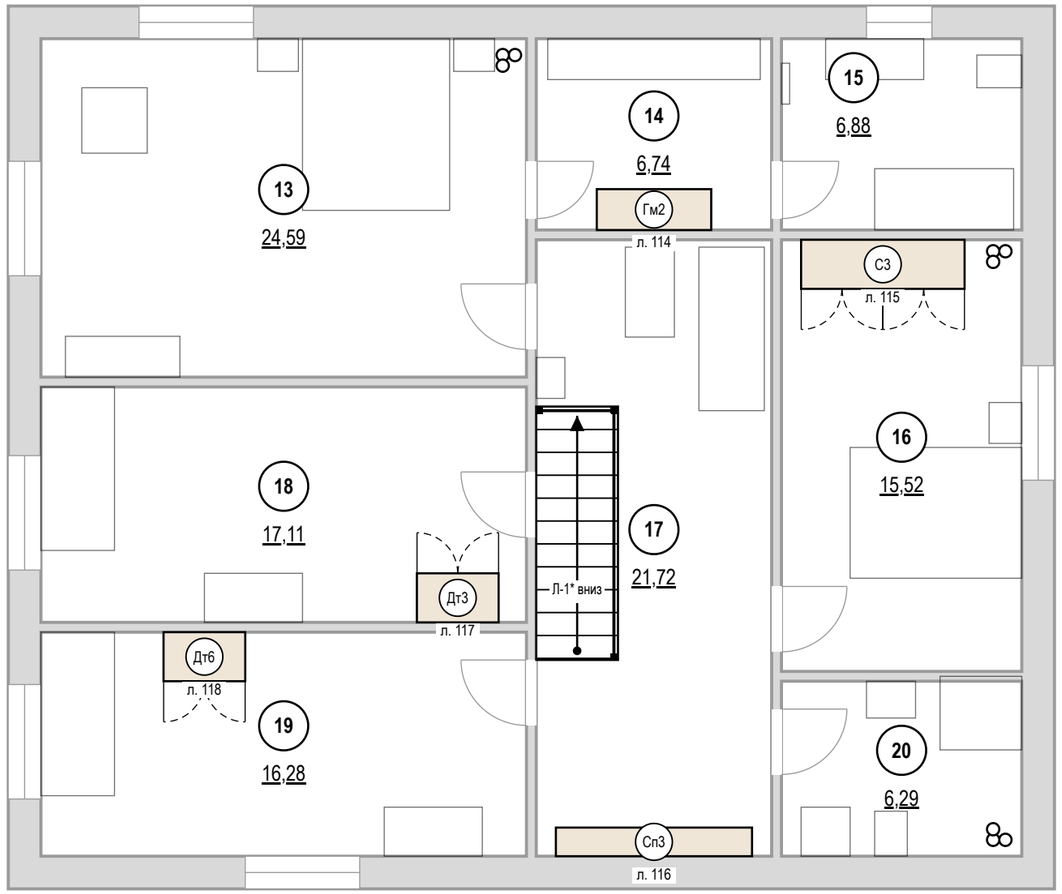

Ведомость изделий

Марка	Наименование	Пом.	Ш×Г×В, мм	Лист
Гм2	Система хранения	14	1400×500×2400	114
С3	Шкаф распашной	16	2000×600×2400	115
Сп3	Система хранения	17	2400×350×900	116
Дт3	Шкаф распашной	18	1000×600×2200	117
Дт6	Шкаф распашной	19	1000×600×2200	118

Условные обозначения

- изделие мебельщика: корпус на полу
- невидимый контур: навесной модуль, корпус под столешницей
- открывание распашного фасада
- зона выдвижения ящика, двери техники
- дверь купе, стрелка — направление движения
- К1 — марка изделия или модуля (на схеме расположения под ней — лист изделия)

Допущения и предложения на листе

Основа листа: размеры и контуры этажей подобраны проектировщиком по составу помещений и площадям этажей с картинки 470 px (размеры на ней не читаются); обмер и исходный проект — задание (К-1); высоты: 1-й этаж 2800 мм, мансарда 2700 мм (горизонтальная часть) приняты; скаты кровли мансарды приняты по картинке: колено 1200 мм, уклон 45°, конёк вдоль длинной стороны; проект КР — задание (К-2); наружные стены 400 мм, перегородки 120 мм приняты (К-1); разрешённая мощность 15 кВт принята по типовым ТУ для частного дома (К-4); подрайон климата не задан — принят не северный (жилые от 2,5 м) (К-7).

Знак «*» — принято, не замерено и не подтверждено (замерить на объекте): К-2: отметка чистого пола этажа «Мансарда» +3,150 — принята без источника, все отметки мансарды считаются от неё; К-6: Л-1 — габарит марша снят с картинки заказчика (11 проступей в холле 3,6 м), а до отм. +3,150 нужно 18 подъёмов — одномаршевая не встаёт: решение по К-6.

См. лист открытых вопросов (лист 8, записи К-1, К-2, К-4, К-6, К-7).

Примечания

1. Изделия — по чистовым размерам помещений; перед раскроем — контрольный замер цеха после чистовой отделки стен, пола и потолка.
2. Открывание фасадов и выдвижение ящиков показано в открытом положении: зоны не пересекают двери, радиаторы, выключатели и проходы.
3. Стояки и счётчики за мебелью — с сервисным люком; газовые трубы мебелью не зашиваются.
4. Покупная мебель — по плану расстановки мебели и спецификации дизайнера; здесь — подложкой.

1000 мм · печать 1:1

Изм.	Кол.уч	Лист	№ док.	Подп.	Дата
Разраб.		Кырлан А.С.			04.11.26
Пров.					
ГИП					
Н. контр.					
Утв.					

ГД-2026-010-АИ

Дом 331 м²

Общая площадь 270,67* м² · * размеры приняты, не замерены (реестр — л. 8–10, К-1)

Дизайн-проект интерьера

Стадия	Лист	Листов
РП	109	216

Встроенная мебель. Схема расположения · Мансарда

М 1:75

Кырлан Александр Сергеевич


выпуск 04.11.2026 № 2a77323a49 · стр. 112 из 221

Система хранения Кт1


Котельная (пом. 4) · вид из помещения · размеры в мм, отметки в м от ±0,000 (чистый пол 1-го этажа)

ПРЕДВАРИТЕЛЬНО · не для производства работ · открыто пунктов: 15 (реестр — л. 8–10)


Общий вид

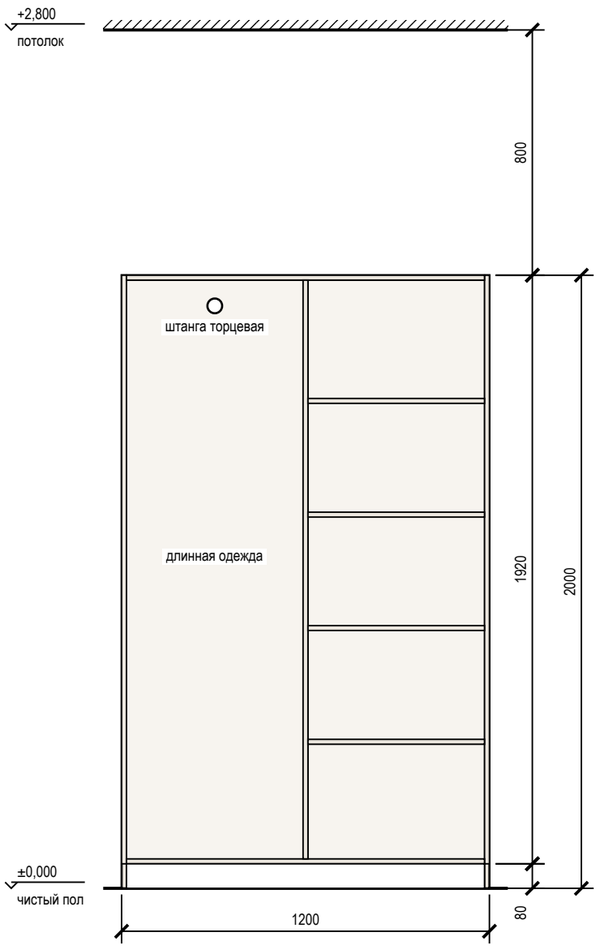


Наполнение, размеры в свету

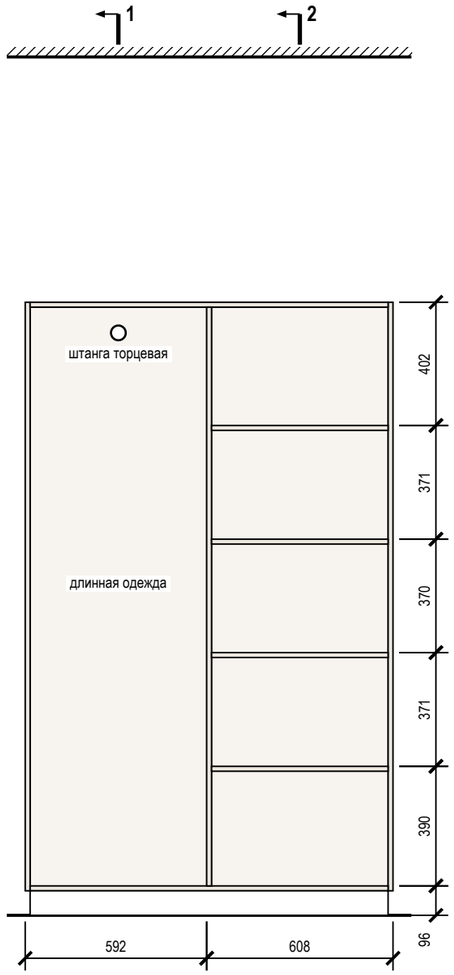

Разрез 1-1

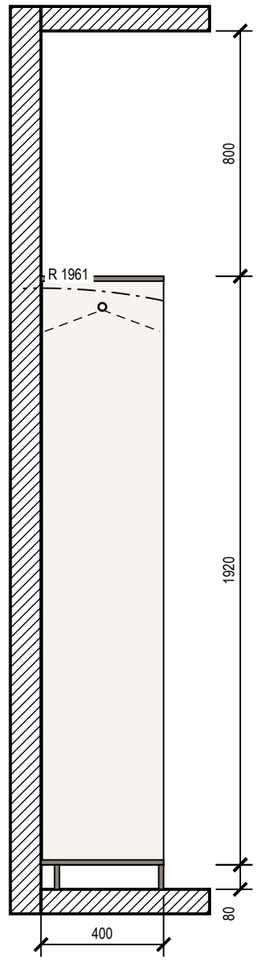

Разрез 2-2

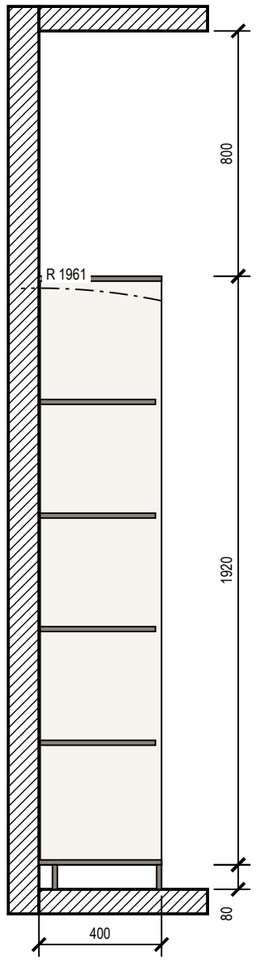

Примечания

1. Размеры — в мм по чистовой отделке; изделие 1200×400×2000 (Ш×Г×В). Перед раскроем — контрольный замер цеха после чистовой отделки стен, пола и потолка.
2. Корпус — ЛДСП 16 мм, задняя стенка ХДФ 4 мм в паз, цоколь 80 мм на регулируемых опорах; открытая система: без фасадов.
3. Кромка: скрытые торцы 0,4 мм, видимые 2 мм (ПВХ/АБС).
4. Присадка по 32-й системе — выполняет цех.
5. Зазор до потолка 800 мм.
6. Подъём корпуса: диагональ боковины без цоколя √(1920² + 400²) = 1961 мм < 2800 мм до потолка — корпус собирается лёжа, поднимается поворотом и ставится на цоколь.
7. Крепление к стене от опрокидывания — уголки 2 шт. к несущему основанию (монтажная схема шкафов).

Условные обозначения

- корпус и полки ЛДСП (вид на стену)
- задняя стенка ХДФ
- деталь в разрезе
- штанга для плечиков (на разрезе — плечики 450 мм)
- траектория угла корпуса при подъёме в проектное положение

Допущения и предложения на листе

Основа листа: размеры и контуры этажей подобраны проектировщиком по составу помещений и площадям этажей с картинки 470 px (размеры на ней не читаются); обмер и исходный проект — задание (К-1); высоты: 1-й этаж 2800 мм, мансарда 2700 мм (горизонтальная часть) приняты; скаты кровли мансарды приняты по картинке: колено 1200 мм, уклон 45°, конёк вдоль длинной стороны; проект КР — задание (К-2); наружные стены 400 мм, перегородки 120 мм приняты (К-1); разрешённая мощность 15 кВт принята по типовым ТУ для частного дома (К-4); подрайон климата не задан — принят не северный (жилые от 2,5 м) (К-7).
См. лист открытых вопросов (лист 8, записи К-1, К-2, К-4, К-7).

1000 мм · печать 1:1

Изм.	Кол.уч	Лист	№ док.	Подп.	Дата
Разраб.		Кырлан А.С.			04.11.26
Пров.					
ГИП					
Н. контр.					
Утв.					

ГД-2026-010-АИ

Дом 331 м²

Общая площадь 270,67* м² · * размеры приняты, не замерены (реестр — л. 8–10, К-1)

Дизайн-проект интерьера

Стадия	Лист	Листов
РП	110	216

Система хранения Кт1

М 1:20

Кырлан Александр Сергеевич


выпуск 04.11.2026 № 2a77323a49 · стр. 113 из 221

Система хранения Кл1


Кладовая (пом. 7) · вид из помещения · размеры в мм, отметки в м от ±0,000 (чистый пол 1-го этажа)

ПРЕДВАРИТЕЛЬНО · не для производства работ · открыто пунктов: 15 (реестр — л. 8–10)


Общий вид

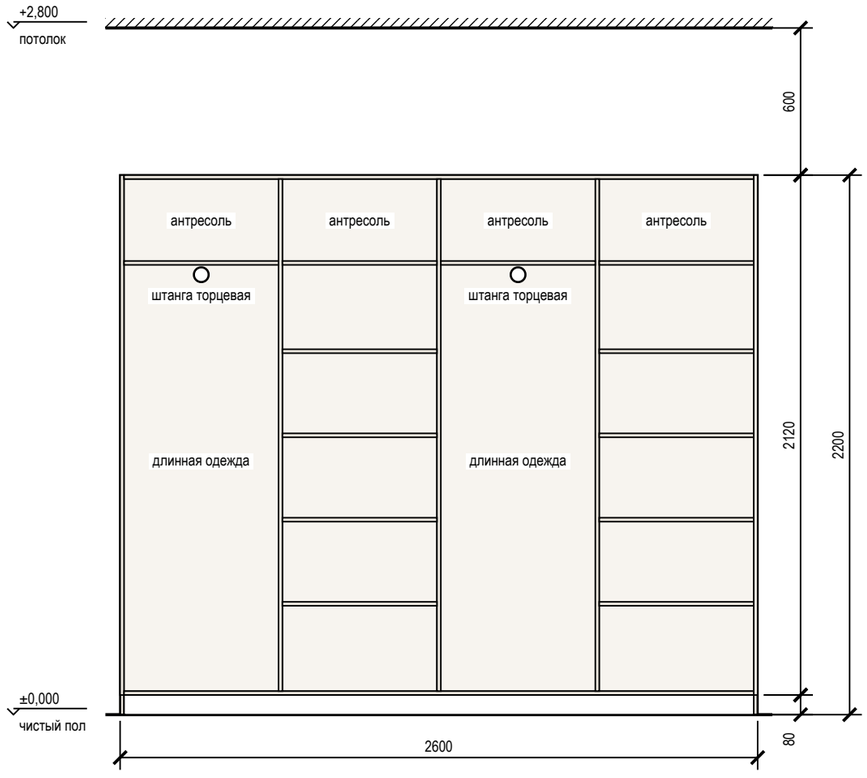


Наполнение, размеры в свету

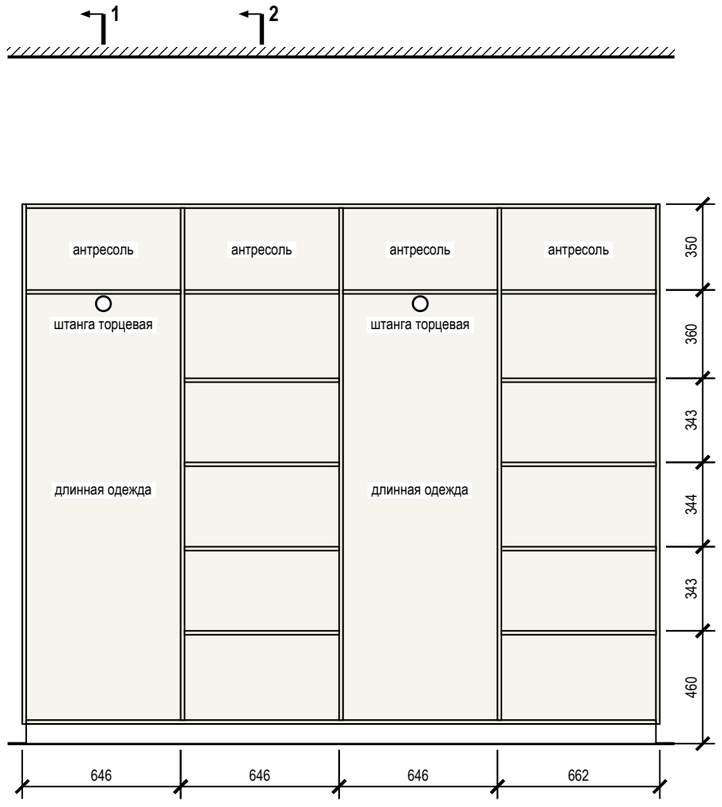

Разрез 1-1

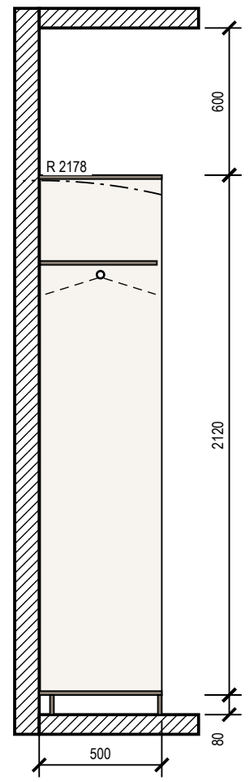

Разрез 2-2

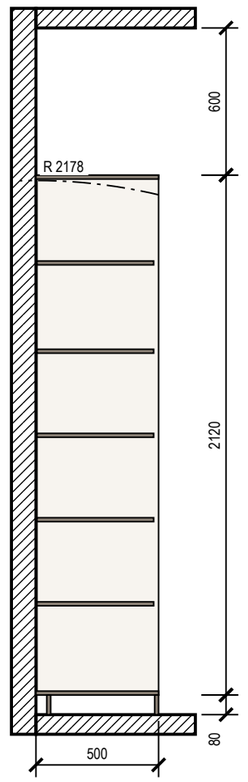

Примечания

1. Размеры — в мм по чистовой отделке; изделие 2600×500×2200 (Ш×Г×В). Перед раскроем — контрольный замер цеха после чистовой отделки стен, пола и потолка.
2. Корпус — ЛДСП 16 мм, задняя стенка ХДФ 4 мм в паз, цоколь 80 мм на регулируемых опорах; открытая система: без фасадов.
3. Кромка: скрытые торцы 0,4 мм, видимые 2 мм (ПВХ/АБС).
4. Присадка по 32-й системе — выполняет цех.
5. Зазор до потолка 600 мм.
6. Подъём корпуса: диагональ боковины без цоколя √(2120² + 500²) = 2178 мм < 2800 мм до потолка — корпус собирается лёжа, поднимается поворотом и ставится на цоколь.
7. Крепление к стене от опрокидывания — уголки 2 шт. к несущему основанию (монтажная схема шкафов).

Условные обозначения

- корпус и полки ЛДСП (вид на стену)
- задняя стенка ХДФ
- деталь в разрезе
- штанга для плечиков (на разрезе — плечики 450 мм)
- траектория угла корпуса при подъёме в проектное положение

Допущения и предложения на листе

Основа листа: размеры и контуры этажей подобраны проектировщиком по составу помещений и площадям этажей с картинки 470 px (размеры на ней не читаются); обмер и исходный проект — задание (К-1); высоты: 1-й этаж 2800 мм, мансарда 2700 мм (горизонтальная часть) приняты; скаты кровли мансарды приняты по картинке: колено 1200 мм, уклон 45°, конёк вдоль длинной стороны; проект КР — задание (К-2); наружные стены 400 мм, перегородки 120 мм приняты (К-1); разрешённая мощность 15 кВт принята по типовым ТУ для частного дома (К-4); подрайон климата не задан — принят не северный (жилые от 2,5 м) (К-7).
См. лист открытых вопросов (лист 8, записи К-1, К-2, К-4, К-7).

1000 мм · печать 1:1

Изм.	Кол.уч	Лист	№ док.	Подп.	Дата
Разраб.		Кырлан А.С.			04.11.26
Пров.					
ГИП					
Н. контр.					
Утв.					

ГД-2026-010-АИ

Дом 331 м²

Общая площадь 270,67* м² · * размеры приняты, не замерены (реестр — л. 8–10, К-1)

Дизайн-проект интерьера

Стадия	Лист	Листов
РП	111	216

Система хранения Кл1

М 1:25

Кырлан Александр Сергеевич


выпуск 04.11.2026 № 2a77323a49 · стр. 114 из 221

Шкаф-купе Пх1


Прихожая (пом. 8) · вид из помещения · размеры в мм, отметки в м от ±0,000 (чистый пол 1-го этажа)

ПРЕДВАРИТЕЛЬНО · не для производства работ · открыто пунктов: 15 (реестр — л. 8–10)


Вид с фасадами

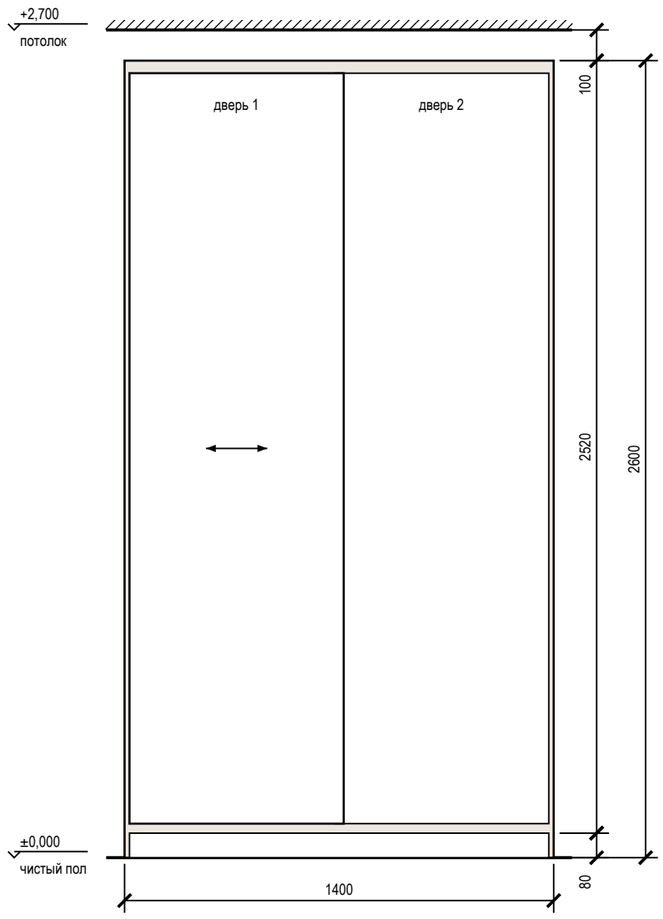


Вид без фасадов

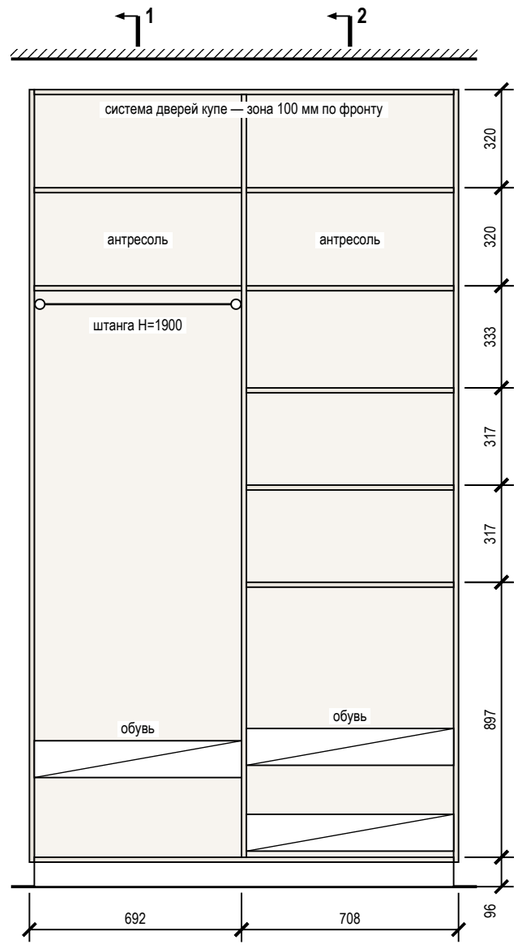

Разрез 1-1

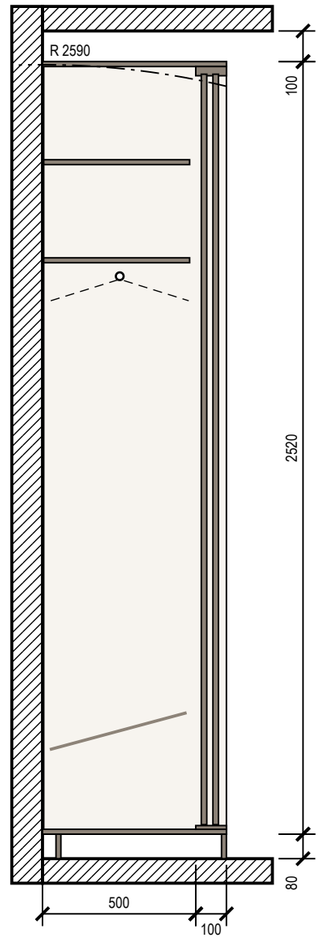

Разрез 2-2

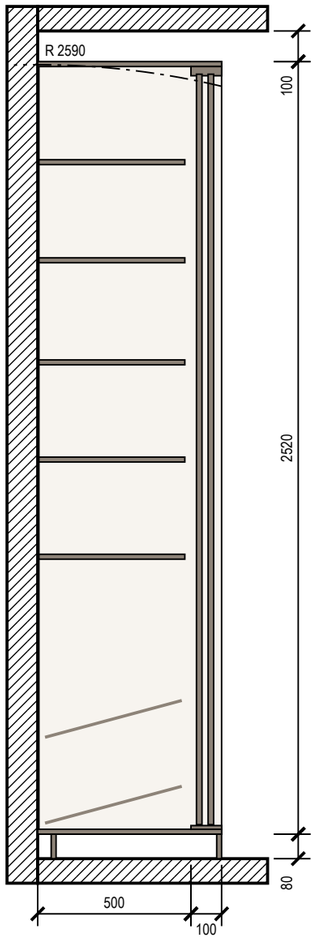

Примечания

1. Размеры — в мм по чистовой отделке; изделие 1400×600×2600 (Ш×Г×В). Перед раскроем — контрольный замер цеха после чистовой отделки стен, пола и потолка.
2. Корпус — ЛДСП 16 мм, задняя стенка ХДФ 4 мм в паз, цоколь 80 мм на регулируемых опорах; двери купе — ЛДСП 10 мм в алюминиевом профиле; нахлёст 30 мм, ширина двери 699 мм, высота — проём минус 40 мм; цвет — по колерной карте.
3. Кромка: скрытые торцы 0,4 мм, видимые 2 мм (ПВХ/АБС).
4. Номинальные зазоры: дверь купе — боковина 3 мм, фасад ящика — стойка 2 мм; ящики внутри купе — с накладкой 30 мм на стойке со стороны нахлёста дверей.
5. Присадка по 32-й системе — выполняет цех.
6. Зазор до потолка 100 мм — закрыть планкой в цвет корпуса при монтаже.
7. Подъём корпуса: диагональ боковины без цоколя √(2520² + 600²) = 2590 мм < 2700 мм до потолка — корпус собирается лёжа, поднимается поворотом и ставится на цоколь.
8. Крепление к стене от опрокидывания — уголки 2 шт. к несущему основанию (монтажная схема шкафов).

Условные обозначения

- дверь купе, стрелка — направление движения
- корпус и полки ЛДСП (вид на стену)
- задняя стенка ХДФ
- деталь в разрезе
- штанга для плечиков (на разрезе — плечики 450 мм)
- траектория угла корпуса при подъёме в проектное положение

Допущения и предложения на листе

Основа листа: размеры и контуры этажей подобраны проектировщиком по составу помещений и площадям этажей с картинки 470 px (размеры на ней не читаются); обмер и исходный проект — задание (К-1); высоты: 1-й этаж 2800 мм, мансарда 2700 мм (горизонтальная часть) приняты; скаты кровли мансарды приняты по картинке: колено 1200 мм, уклон 45°, конёк вдоль длинной стороны; проект КР — задание (К-2); наружные стены 400 мм, перегородки 120 мм приняты (К-1); разрешённая мощность 15 кВт принята по типовым ТУ для частного дома (К-4); подрайон климата не задан — принят не северный (жилые от 2,5 м) (К-7).
См. лист открытых вопросов (лист 8, записи К-1, К-2, К-4, К-7).

1000 мм · печать 1:1

Изм.	Кол.уч	Лист	№ док.	Подп.	Дата
Разраб.		Кырлан А.С.			04.11.26
Пров.					
ГИП					
Н. контр.					
Утв.					

ГД-2026-010-АИ

Дом 331 м²

Общая площадь 270,67* м² · * размеры приняты, не замерены (реестр — л. 8–10, К-1)

Дизайн-проект интерьера

Стадия	Лист	Листов
РП	112	216

Шкаф-купе Пх1

М 1:20

Кырлан Александр Сергеевич


выпуск 04.11.2026 № 2a77323a49 · стр. 115 из 221

Система хранения Гр1


Гараж (пом. 10) · вид из помещения · размеры в мм, отметки в м от ±0,000 (чистый пол 1-го этажа)

ПРЕДВАРИТЕЛЬНО · не для производства работ · открыто пунктов: 15 (реестр — л. 8–10)


Общий вид

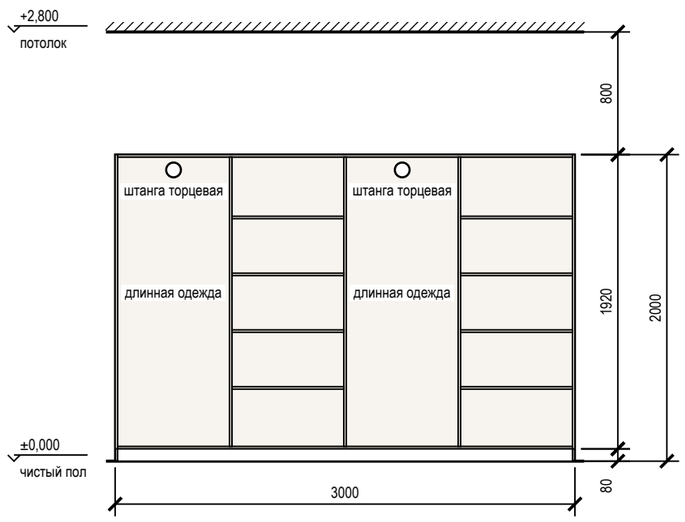


Наполнение, размеры в свету

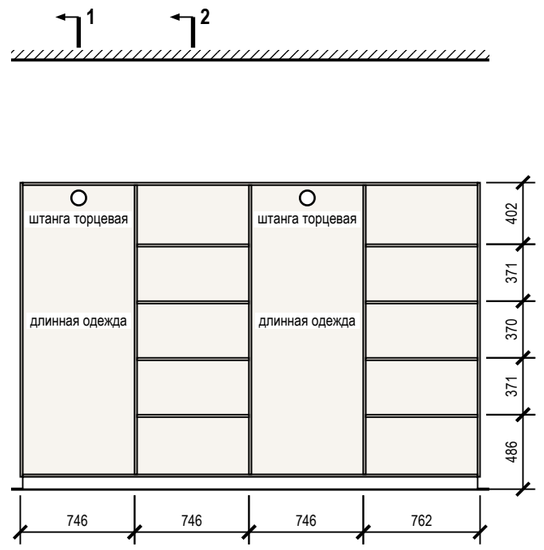

Разрез 1-1

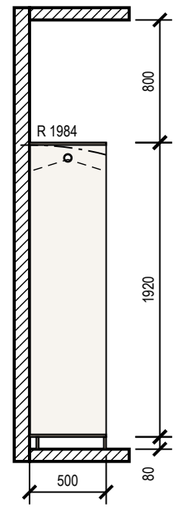

Разрез 2-2

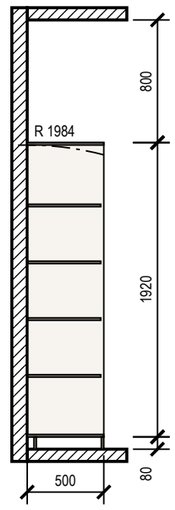

Примечания

1. Размеры — в мм по чистовой отделке; изделие 3000×500×2000 (Ш×Г×В). Перед раскроем — контрольный замер цеха после чистовой отделки стен, пола и потолка.
2. Корпус — ЛДСП 16 мм, задняя стенка ХДФ 4 мм в паз, цоколь 80 мм на регулируемых опорах; открытая система: без фасадов.
3. Кромка: скрытые торцы 0,4 мм, видимые 2 мм (ПВХ/АБС).
4. Присадка по 32-й системе — выполняет цех.
5. Зазор до потолка 800 мм.
6. Подъём корпуса: диагональ боковины без цоколя $\sqrt{(1920^2 + 500^2)} = 1984$ мм < 2800 мм до потолка — корпус собирается лёжа, поднимается поворотом и ставится на цоколь.
7. Крепление к стене от опрокидывания — уголки 2 шт. к несущему основанию (монтажная схема шкафов).

Условные обозначения

- корпус и полки ЛДСП (вид на стену)
- задняя стенка ХДФ
- деталь в разрезе
- штанга для плечиков (на разрезе — плечики 450 мм)
- траектория угла корпуса при подъёме в проектное положение

Допущения и предложения на листе

Основа листа: размеры и контуры этажей подобраны проектировщиком по составу помещений и площадям этажей с картинки 470 px (размеры на ней не читаются); обмер и исходный проект — задание (К-1); высоты: 1-й этаж 2800 мм, мансарда 2700 мм (горизонтальная часть) приняты; скаты кровли мансарды приняты по картинке: колено 1200 мм, уклон 45°, конёк вдоль длинной стороны; проект КР — задание (К-2); наружные стены 400 мм, перегородки 120 мм приняты (К-1); разрешённая мощность 15 кВт принята по типовым ТУ для частного дома (К-4); подрайон климата не задан — принят не северный (жилые от 2,5 м) (К-7).
См. лист открытых вопросов (лист 8, записи К-1, К-2, К-4, К-7).

1000 мм · печать 1:1

Изм.	Кол.уч	Лист	№ док.	Подп.	Дата
Разраб.		Кырлан А.С.			04.11.26
Пров.					
ГИП					
Н. контр.					
Утв.					

ГД-2026-010-АИ

Дом 331 м²

Общая площадь 270,67* м² · * размеры приняты, не замерены (реестр — л. 8–10, К-1)

Дизайн-проект интерьера

Стадия	Лист	Листов
РП	113	216

Система хранения Гр1

М 1:40

Кырлан Александр Сергеевич


выпуск 04.11.2026 № 2a77323a49 · стр. 116 из 221

Система хранения Гм2


Гардеробная мастер (пом. 14) · вид из помещения · размеры в мм, отметки в м от ±0,000 (чистый пол 1-го этажа)

ПРЕДВАРИТЕЛЬНО · не для производства работ · открыто пунктов: 15 (реестр — л. 8–10)


Общий вид

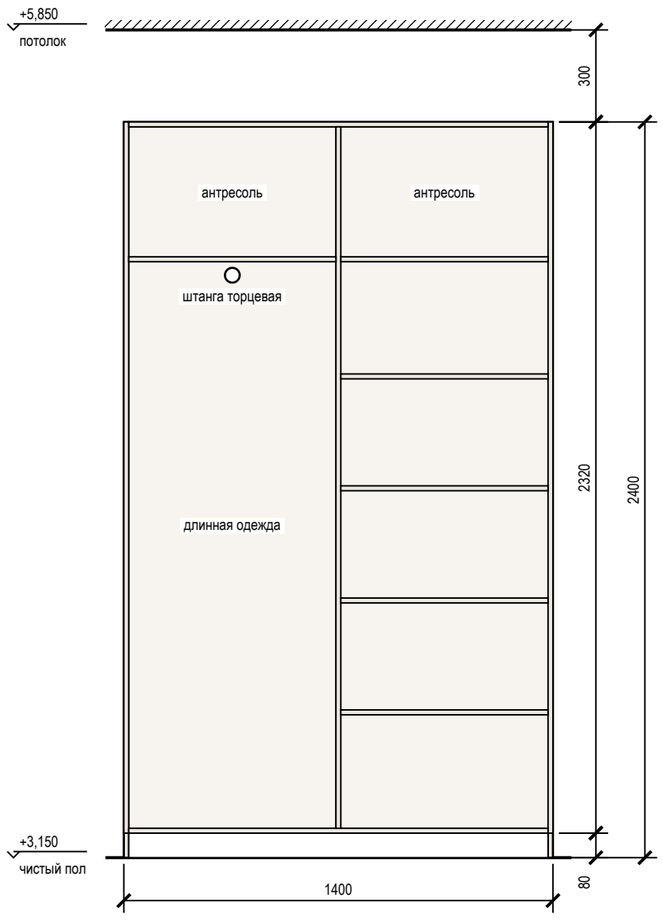


Наполнение, размеры в свету

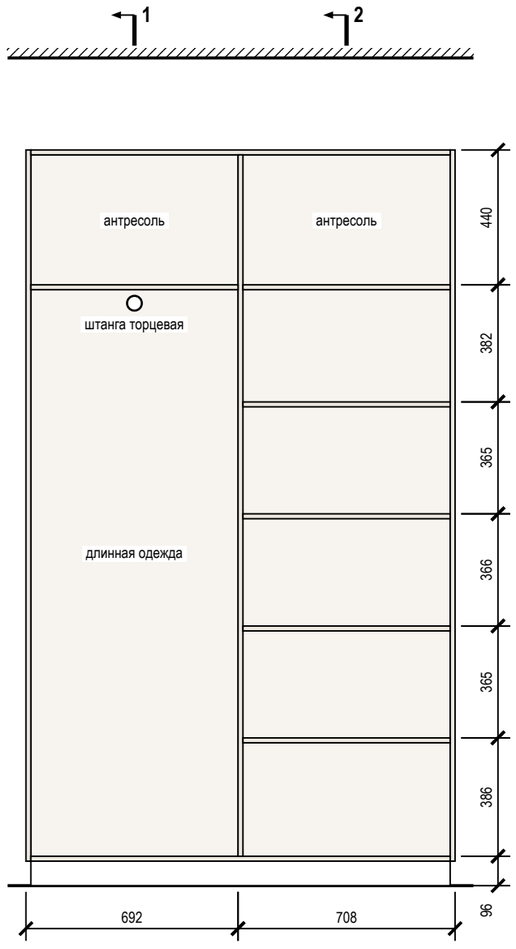

Разрез 1-1

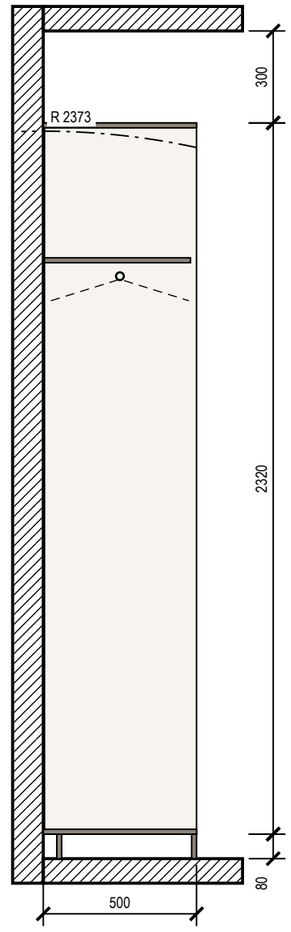

Разрез 2-2

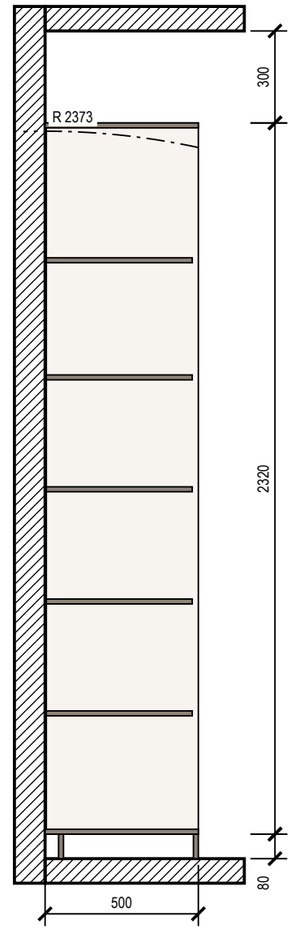

Примечания

1. Размеры — в мм по чистовой отделке; изделие 1400×500×2400 (Ш×Г×В). Перед раскроем — контрольный замер цеха после чистовой отделки стен, пола и потолка.
2. Корпус — ЛДСП 16 мм, задняя стенка ХДФ 4 мм в паз, цоколь 80 мм на регулируемых опорах; открытая система: без фасадов.
3. Кромка: скрытые торцы 0,4 мм, видимые 2 мм (ПВХ/АБС).
4. Присадка по 32-й системе — выполняет цех.
5. Зазор до потолка 300 мм.
6. Подъём корпуса: диагональ боковины без цоколя √(2320² + 500²) = 2373 мм < 2700 мм до потолка — корпус собирается лёжа, поднимается поворотом и ставится на цоколь.
7. Крепление к стене от опрокидывания — уголки 2 шт. к несущему основанию (монтажная схема шкафов).

Условные обозначения

- корпус и полки ЛДСП (вид на стену)
- задняя стенка ХДФ
- деталь в разрезе
- штанга для плечиков (на разрезе — плечики 450 мм)
- траектория угла корпуса при подъёме в проектное положение

Допущения и предложения на листе

Основа листа: размеры и контуры этажей подобраны проектировщиком по составу помещений и площадям этажей с картинки 470 px (размеры на ней не читаются); обмер и исходный проект — задание (К-1); высоты: 1-й этаж 2800 мм, мансарда 2700 мм (горизонтальная часть) приняты; скаты кровли мансарды приняты по картинке: колено 1200 мм, уклон 45°, конёк вдоль длинной стороны; проект КР — задание (К-2); наружные стены 400 мм, перегородки 120 мм приняты (К-1); разрешённая мощность 15 кВт принята по типовым ТУ для частного дома (К-4); подрайон климата не задан — принят не северный (жилые от 2,5 м) (К-7).

Знак «*» — принято, не замерено и не подтверждено (замерить на объекте): К-2: отметка чистого пола этажа «Мансарда» +3,150 — принята без источника, все отметки мансарды считаются от неё.

См. лист открытых вопросов (лист 8, записи К-1, К-2, К-4, К-7).

1000 мм · печать 1:1

Изм.	Кол.уч	Лист	№ док.	Подп.	Дата
Разраб.		Кырлан А.С.			04.11.26
Пров.					
ГИП					
Н. контр.					
Утв.					

ГД-2026-010-АИ

Дом 331 м²

Общая площадь 270,67* м² · * размеры приняты, не замерены (реестр — л. 8–10, К-1)

Дизайн-проект интерьера

Стадия	Лист	Листов
РП	114	216

Система хранения Гм2

М 1:20

Кырлан Александр Сергеевич


выпуск 04.11.2026 № 2a77323a49 · стр. 117 из 221

Шкаф распашной С3


Спальня 2 (пом. 16) · вид из помещения · размеры в мм, отметки в м от ±0,000 (чистый пол 1-го этажа)

ПРЕДВАРИТЕЛЬНО · не для производства работ · открыто пунктов: 15 (реестр — л. 8–10)


Вид с фасадами

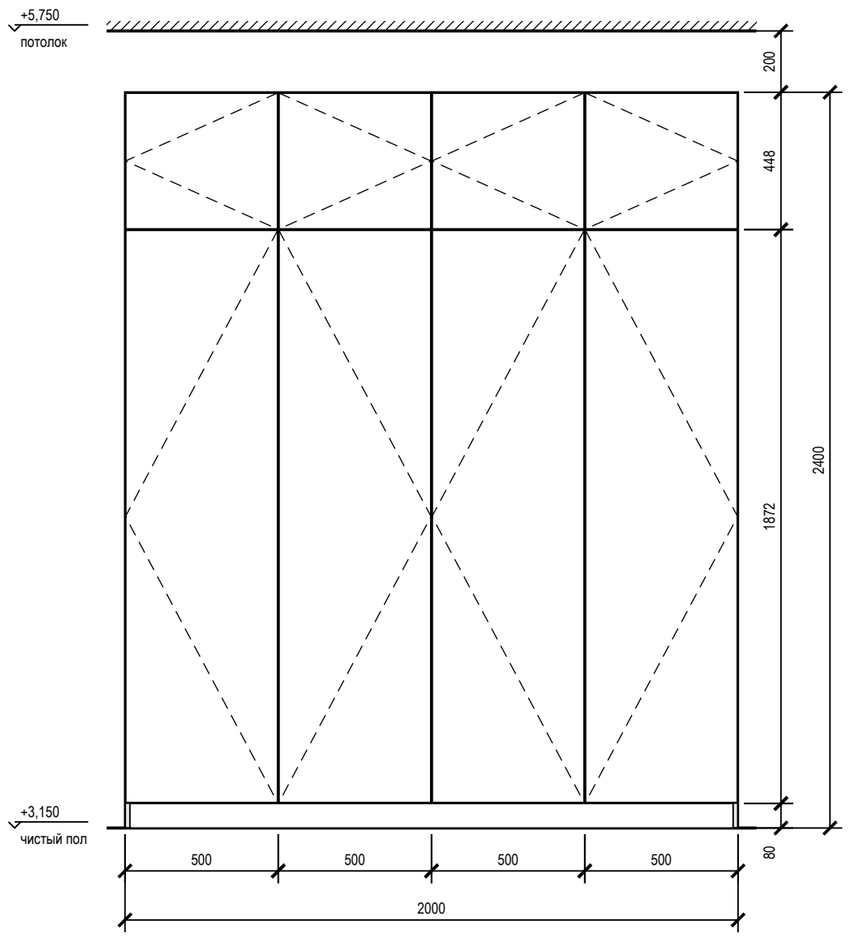


Вид без фасадов

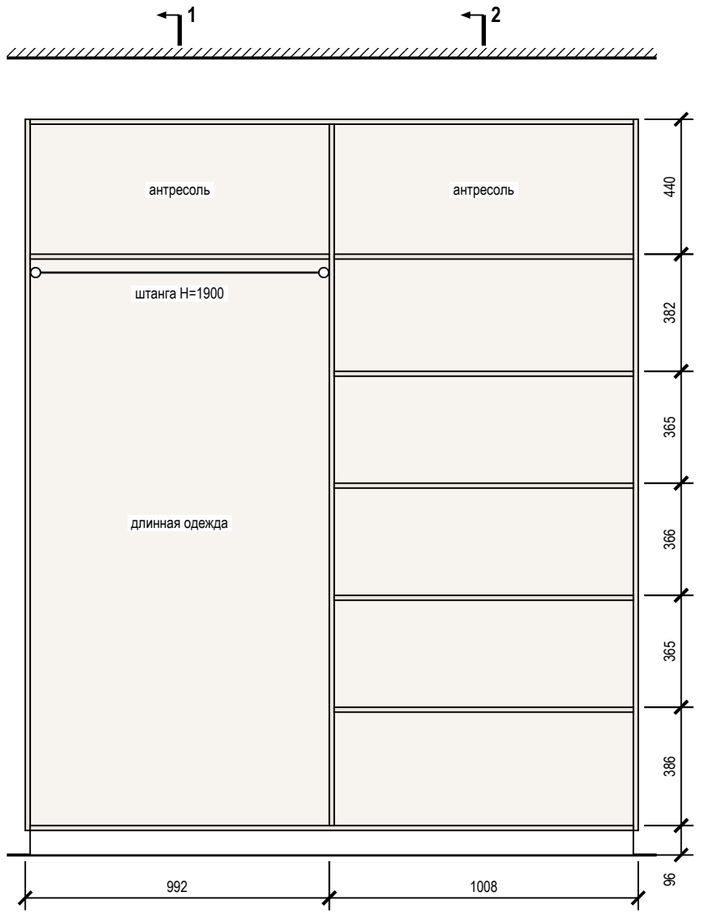

Разрез 1-1

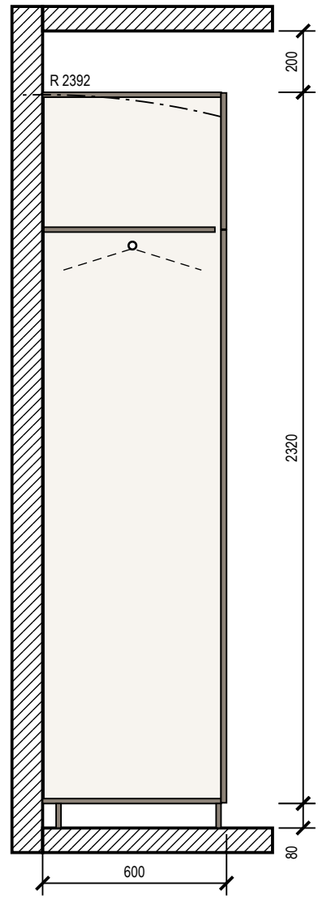

Разрез 2-2

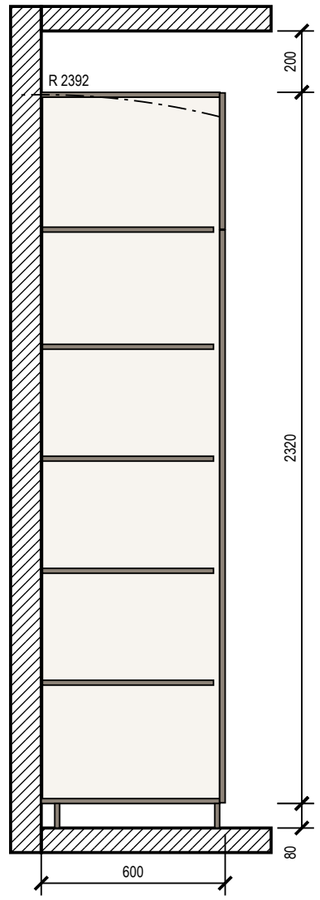

Примечания

1. Размеры — в мм по чистовой отделке; изделие 2000×600×2400 (Ш×Г×В). Перед раскроем — контрольный замер цеха после чистовой отделки стен, пола и потолка.
2. Корпус — ЛДСП 16 мм, задняя стенка ХДФ 4 мм в паз, цоколь 80 мм на регулируемых опорах; фасады накладные — МДФ 18 мм, эмаль матовая, 18 мм; цвет — по колерной карте; петли с доводчиком: фасад 1869 мм — 4 петли, фасад 445 мм — 2 петли.
3. Кромка: скрытые торцы 0,4 мм, видимые 2 мм (ПВХ/АБС).
4. Номинальные зазоры: между фасадами 3 мм, фасад — стена и фасад — потолок не менее 3 мм, фасад ящика — стойка 2 мм.
5. Присадка по 32-й системе — выполняет цех.
6. Зазор до потолка 200 мм.
7. Подъём корпуса: диагональ боковины без цоколя $\sqrt{(2320^2 + 582^2)} = 2392$ мм < 2600 мм до потолка — корпус собирается лёжа, поднимается поворотом и ставится на цоколь.
8. Крепление к стене от опрокидывания — уголки 2 шт. к несущему основанию (монтажная схема шкафов).

Условные обозначения

- фасад распашной: линии сходятся к стороне петель
- корпус и полки ЛДСП (вид на стену)
- задняя стенка ХДФ
- деталь в разрезе
- штанга для плечиков (на разрезе — плечики 450 мм)
- траектория угла корпуса при подъёме в проектное положение

Допущения и предложения на листе

Основа листа: размеры и контуры этажей подобраны проектировщиком по составу помещений и площадям этажей с картинки 470 px (размеры на ней не читаются); обмер и исходный проект — задание (К-1); высоты: 1-й этаж 2800 мм, мансарда 2700 мм (горизонтальная часть) приняты; скаты кровли мансарды приняты по картинке: колено 1200 мм, уклон 45°, конёк вдоль длинной стороны; проект КР — задание (К-2); наружные стены 400 мм, перегородки 120 мм приняты (К-1); разрешённая мощность 15 кВт принята по типовым ТУ для частного дома (К-4); подрайон климата не задан — принят не северный (жилые от 2,5 м) (К-7).

Знак «*» — принято, не замерено и не подтверждено (замерить на объекте): К-2: отметка чистого пола этажа «Мансарда» +3,150 — принята без источника, все отметки мансарды считаются от неё.

См. лист открытых вопросов (лист 8, записи К-1, К-2, К-4, К-7).

1000 мм · печать 1:1

Изм.	Кол.уч	Лист	№ док.	Подп.	Дата
Разраб.		Кырлан А.С.			04.11.26
Пров.					
ГИП					
Н. контр.					
Утв.					

ГД-2026-010-АИ

Дом 331 м²

Общая площадь 270,67* м² · * размеры приняты, не замерены (реестр — л. 8–10, К-1)

Дизайн-проект интерьера

Стадия	Лист	Листов
РП	115	216

Шкаф распашной С3

М 1:20

Кырлан Александр Сергеевич


выпуск 04.11.2026 № 2a77323a49 · стр. 118 из 221

Система хранения Сп3


Холл мансарды (пом. 17) · вид из помещения · размеры в мм, отметки в м от ±0,000 (чистый пол 1-го этажа)

ПРЕДВАРИТЕЛЬНО · не для производства работ · открыто пунктов: 15 (реестр — л. 8–10)


Общий вид

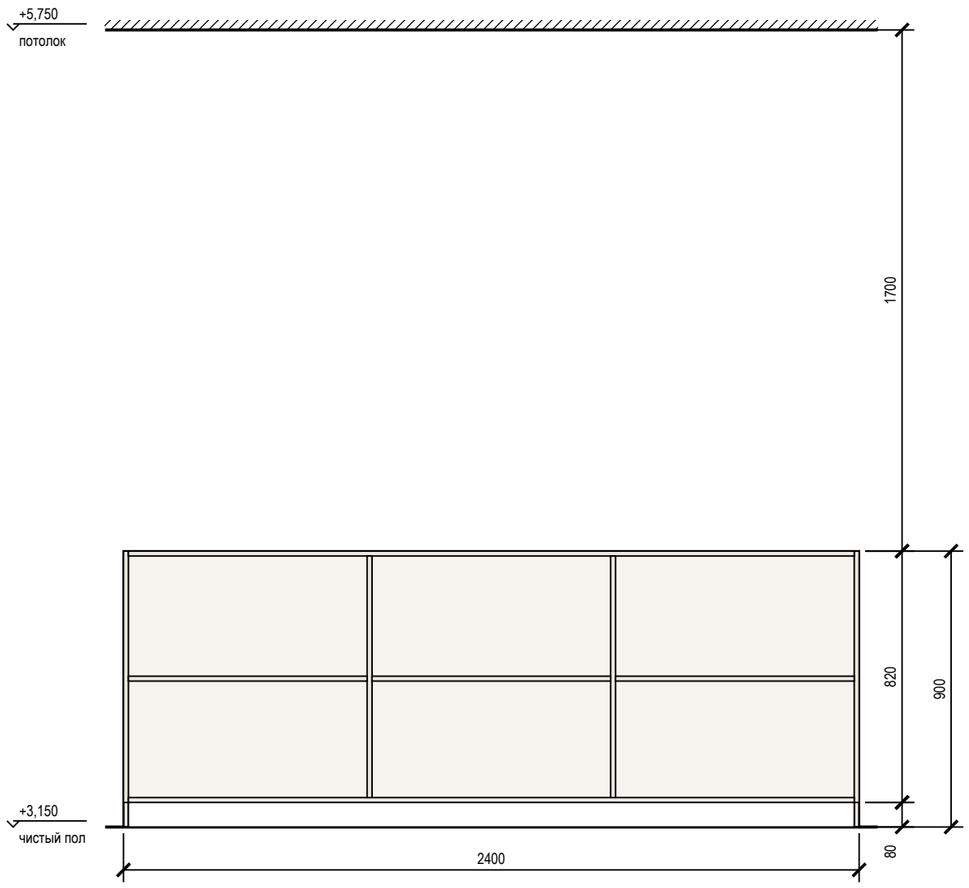

Наполнение, размеры в свету

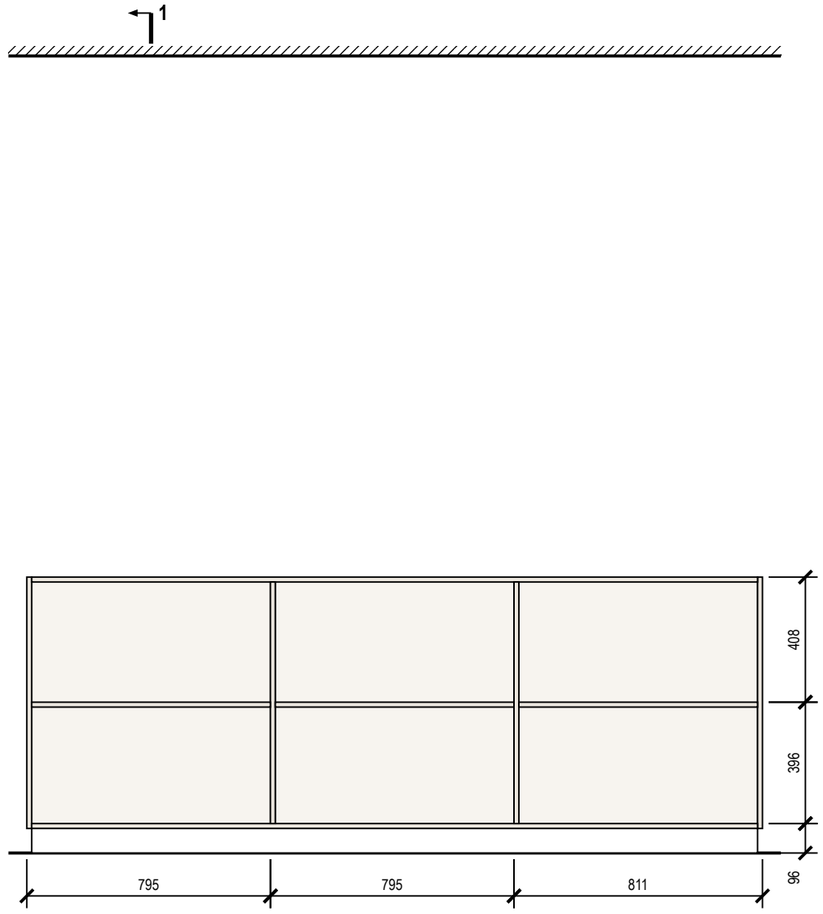

Разрез 1-1

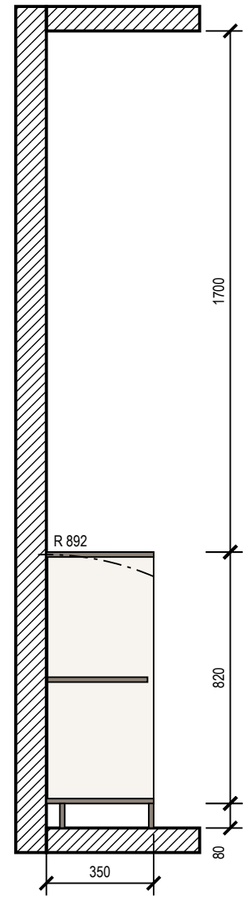

Примечания

1. Размеры — в мм по чистовой отделке; изделие 2400×350×900 (Ш×Г×В). Перед раскроем — контрольный замер цеха после чистовой отделки стен, пола и потолка.
2. Корпус — ЛДСП 16 мм, задняя стенка ХДФ 4 мм в паз, цоколь 80 мм на регулируемых опорах; открытая система: без фасадов.
3. Кромка: скрытые торцы 0,4 мм, видимые 2 мм (ПВХ/АБС).
4. Присадка по 32-й системе — выполняет цех.
5. Зазор до потолка 1700 мм.
6. Подъём корпуса: диагональ боковины без цоколя √(820² + 350²) = 892 мм < 2600 мм до потолка — корпус собирается лёжа, поднимается поворотом и ставится на цоколь.
7. Крепление к стене от опрокидывания — уголки 2 шт. к несущему основанию (монтажная схема шкафов).

Условные обозначения

- корпус и полки ЛДСП (вид на стену)
- задняя стенка ХДФ
- деталь в разрезе
- штанга для плечиков (на разрезе — плечики 450 мм)
- траектория угла корпуса при подъёме в проектное положение

Допущения и предложения на листе

Основа листа: размеры и контуры этажей подобраны проектировщиком по составу помещений и площадям этажей с картинки 470 px (размеры на ней не читаются); обмер и исходный проект — задание (К-1); высоты: 1-й этаж 2800 мм, мансарда 2700 мм (горизонтальная часть) приняты; скаты кровли мансарды приняты по картинке: колено 1200 мм, уклон 45°, конёк вдоль длинной стороны; проект КР — задание (К-2); наружные стены 400 мм, перегородки 120 мм приняты (К-1); разрешённая мощность 15 кВт принята по типовым ТУ для частного дома (К-4); подрайон климата не задан — принят не северный (жилые от 2,5 м) (К-7).

Знак «*» — принято, не замерено и не подтверждено (замерить на объекте): К-2: отметка чистого пола этажа «Мансарда» +3,150 — принята без источника, все отметки мансарды считаются от неё.

См. лист открытых вопросов (лист 8, записи К-1, К-2, К-4, К-7).

1000 мм · печать 1:1

Изм.	Кол.уч	Лист	№ док.	Подп.	Дата
Разраб.		Кырлан А.С.			04.11.26
Пров.					
ГИП					
Н. контр.					
Утв.					

ГД-2026-010-АИ

Дом 331 м²

Общая площадь 270,67* м² · * размеры приняты, не замерены (реестр — л. 8–10, К-1)

Дизайн-проект интерьера

Стадия	Лист	Листов
РП	116	216

Система хранения Сп3

М 1:20

Кырлан Александр Сергеевич


выпуск 04.11.2026 · 2a77323a49 · стр. 119 из 221

Шкаф распашной Дт3


Спальня 3 (пом. 18) · вид из помещения · размеры в мм, отметки в м от ±0,000 (чистый пол 1-го этажа)

ПРЕДВАРИТЕЛЬНО · не для производства работ · открыто пунктов: 15 (реестр — л. 8–10)


Вид с фасадами

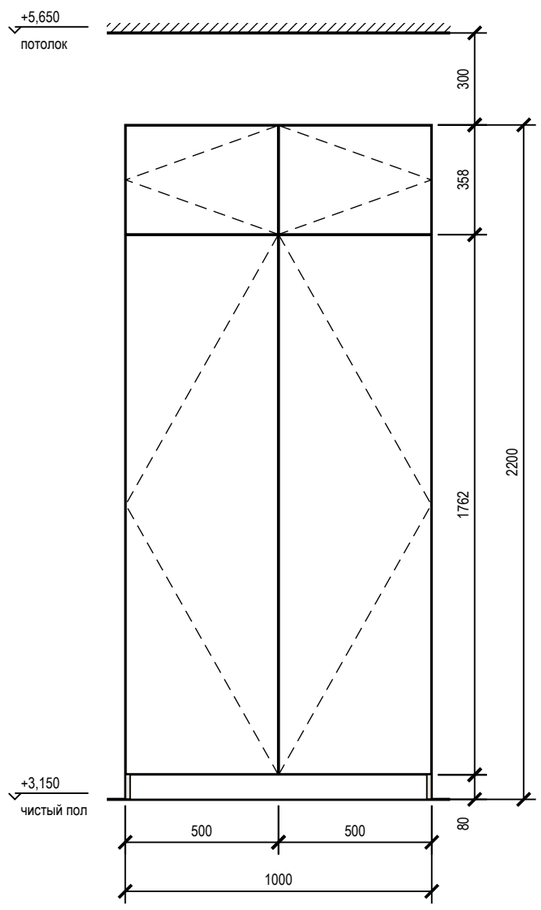

Вид без фасадов

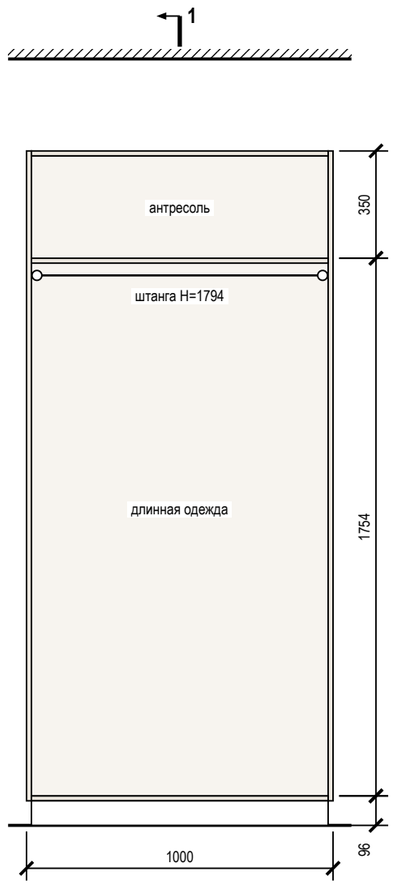

Разрез 1-1

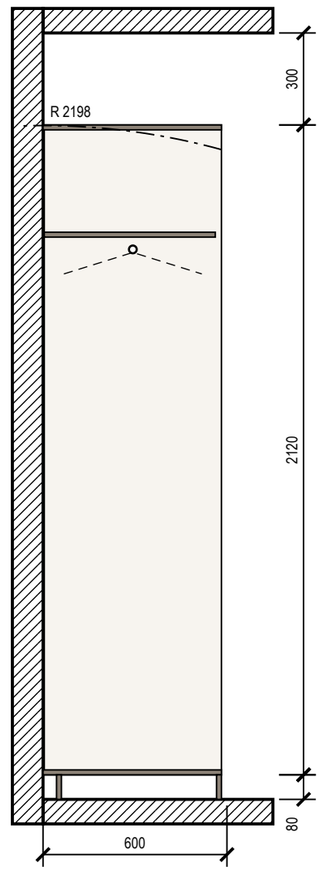

Примечания

1. Размеры — в мм по чистовой отделке; изделие 1000×600×2200 (Ш×Г×В). Перед раскроем — контрольный замер цеха после чистовой отделки стен, пола и потолка.
2. Корпус — ЛДСП 16 мм, задняя стенка ХДФ 4 мм в паз, цоколь 80 мм на регулируемых опорах; фасады накладные — МДФ 18 мм, эмаль матовая, 18 мм; цвет — по колерной карте; петли с доводчиком: фасад 1759 мм — 4 петли, фасад 355 мм — 2 петли.
3. Кромка: скрытые торцы 0,4 мм, видимые 2 мм (ПВХ/АБС).
4. Номинальные зазоры: между фасадами 3 мм, фасад — стена и фасад — потолок не менее 3 мм, фасад ящика — стойка 2 мм.
5. Присадка по 32-й системе — выполняет цех.
6. Зазор до потолка 300 мм.
7. Подъём корпуса: диагональ боковины без цоколя $\sqrt{(2120^2 + 582^2)} = 2198$ мм < 2500 мм до потолка — корпус собирается лёжа, поднимается поворотом и ставится на цоколь.
8. Крепление к стене от опрокидывания — уголки 2 шт. к несущему основанию (монтажная схема шкафов).

Условные обозначения

- фасад распашной: линии сходятся к стороне петель
- корпус и полки ЛДСП (вид на стену)
- задняя стенка ХДФ
- деталь в разрезе
- штанга для плечиков (на разрезе — плечики 450 мм)
- траектория угла корпуса при подъёме в проектное положение

Допущения и предложения на листе

Основа листа: размеры и контуры этажей подобраны проектировщиком по составу помещений и площадям этажей с картинки 470 px (размеры на ней не читаются); обмер и исходный проект — задание (К-1); высоты: 1-й этаж 2800 мм, мансарда 2700 мм (горизонтальная часть) приняты; скаты кровли мансарды приняты по картинке: колено 1200 мм, уклон 45°, конёк вдоль длинной стороны; проект КР — задание (К-2); наружные стены 400 мм, перегородки 120 мм приняты (К-1); разрешённая мощность 15 кВт принята по типовым ТУ для частного дома (К-4); подрайон климата не задан — принят не северный (жилые от 2,5 м) (К-7).

Знак «*» — принято, не замерено и не подтверждено (замерить на объекте): К-2: отметка чистого пола этажа «Мансарда» +3,150 — принята без источника, все отметки мансарды считаются от неё.

См. лист открытых вопросов (лист 8, записи К-1, К-2, К-4, К-7).

1000 мм · печать 1:1

Изм.	Кол.уч	Лист	№ док.	Подп.	Дата
Разраб.		Кырлан А.С.			04.11.26
Пров.					
ГИП					
Н. контр.					
Утв.					

ГД-2026-010-АИ

Дом 331 м²

Общая площадь 270,67* м² · * размеры приняты, не замерены (реестр — л. 8–10, К-1)

Дизайн-проект интерьера

Стадия	Лист	Листов
РП	117	216

Шкаф распашной Дт3

М 1:20

Кырлан Александр Сергеевич


выпуск 04.11.2026 № 2a77323a49 · стр. 120 из 221

Шкаф распашной Дт6


Спальня 4 (пом. 19) · вид из помещения · размеры в мм, отметки в м от ±0,000 (чистый пол 1-го этажа)

ПРЕДВАРИТЕЛЬНО · не для производства работ · открыто пунктов: 15 (реестр — л. 8–10)


Вид с фасадами

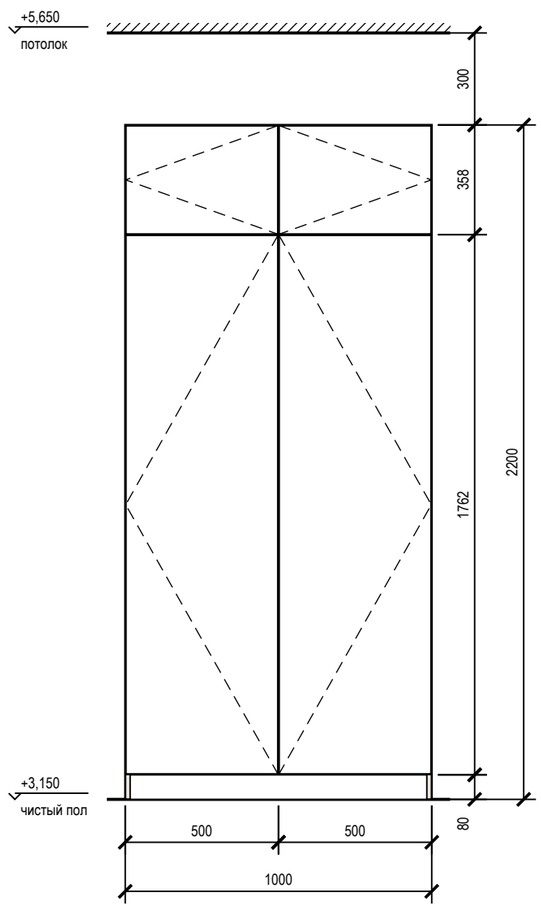

Вид без фасадов

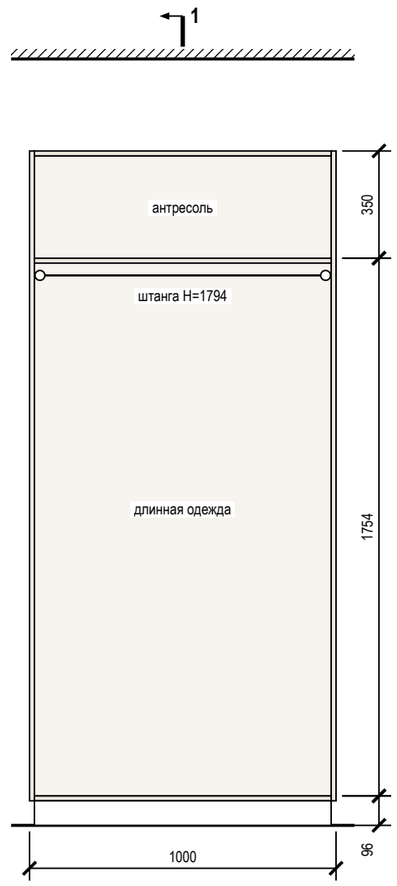

Разрез 1-1

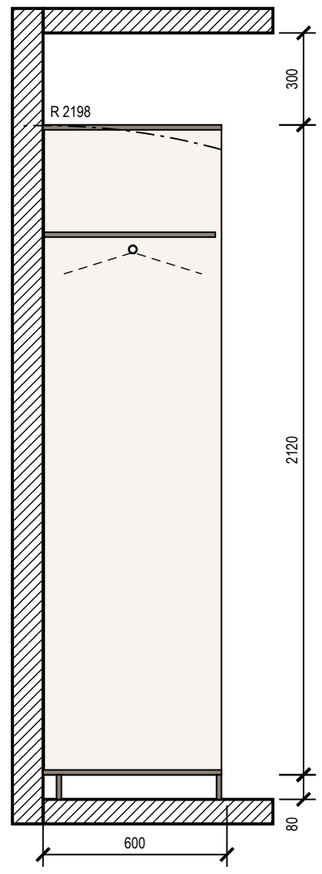

Примечания

1. Размеры — в мм по чистовой отделке; изделие 1000×600×2200 (Ш×Г×В). Перед раскроем — контрольный замер цеха после чистовой отделки стен, пола и потолка.
2. Корпус — ЛДСП 16 мм, задняя стенка ХДФ 4 мм в паз, цоколь 80 мм на регулируемых опорах; фасады накладные — МДФ 18 мм, эмаль матовая, 18 мм; цвет — по колерной карте; петли с доводчиком: фасад 1759 мм — 4 петли, фасад 355 мм — 2 петли.
3. Кромка: скрытые торцы 0,4 мм, видимые 2 мм (ПВХ/АБС).
4. Номинальные зазоры: между фасадами 3 мм, фасад — стена и фасад — потолок не менее 3 мм, фасад ящика — стойка 2 мм.
5. Присадка по 32-й системе — выполняет цех.
6. Зазор до потолка 300 мм.
7. Подъём корпуса: диагональ боковины без цоколя $\sqrt{(2120^2 + 582^2)} = 2198$ мм < 2500 мм до потолка — корпус собирается лёжа, поднимается поворотом и ставится на цоколь.
8. Крепление к стене от опрокидывания — уголки 2 шт. к несущему основанию (монтажная схема шкафов).

Условные обозначения

- фасад распашной: линии сходятся к стороне петель
- корпус и полки ЛДСП (вид на стену)
- задняя стенка ХДФ
- деталь в разрезе
- штанга для плечиков (на разрезе — плечики 450 мм)
- траектория угла корпуса при подъёме в проектное положение

Допущения и предложения на листе

Основа листа: размеры и контуры этажей подобраны проектировщиком по составу помещений и площадям этажей с картинки 470 px (размеры на ней не читаются); обмер и исходный проект — задание (К-1); высоты: 1-й этаж 2800 мм, мансарда 2700 мм (горизонтальная часть) приняты; скаты кровли мансарды приняты по картинке: колено 1200 мм, уклон 45°, конёк вдоль длинной стороны; проект КР — задание (К-2); наружные стены 400 мм, перегородки 120 мм приняты (К-1); разрешённая мощность 15 кВт принята по типовым ТУ для частного дома (К-4); подрайон климата не задан — принят не северный (жилые от 2,5 м) (К-7).

Знак «*» — принято, не замерено и не подтверждено (замерить на объекте): К-2: отметка чистого пола этажа «Мансарда» +3,150 — принята без источника, все отметки мансарды считаются от неё.

См. лист открытых вопросов (лист 8, записи К-1, К-2, К-4, К-7).

1000 мм · печать 1:1

Изм.	Кол.уч	Лист	№ док.	Подп.	Дата
Разраб.		Кырлан А.С.			04.11.26
Пров.					
ГИП					
Н. контр.					
Утв.					

ГД-2026-010-АИ

Дом 331 м²

Общая площадь 270,67* м² · * размеры приняты, не замерены (реестр — л. 8–10, К-1)

Дизайн-проект интерьера

Стадия	Лист	Листов
РП	118	216

Шкаф распашной Дт6

М 1:20


Кырлан Александр Сергеевич

выпуск 04.11.2026 № 2a77323a49 · стр. 121 из 221


Кухня (пом. 1). Развёртка гарнитура

Кухня-столовая (пом. 1) · стена А · вид из помещения · размеры в мм, отметки в м от ±0,000 (чистый пол 1-го этажа)


Вид с фасадами

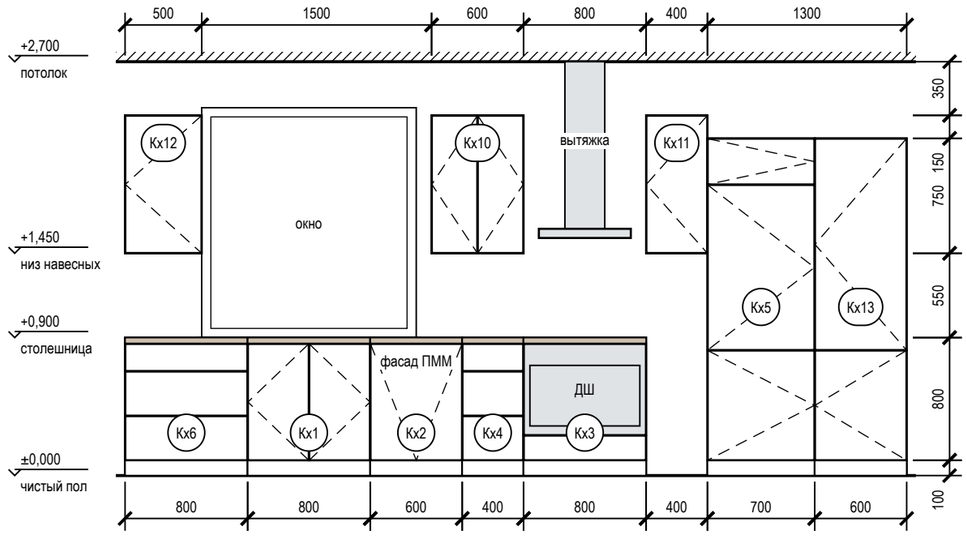


Вид без фасадов (наполнение, выводы)

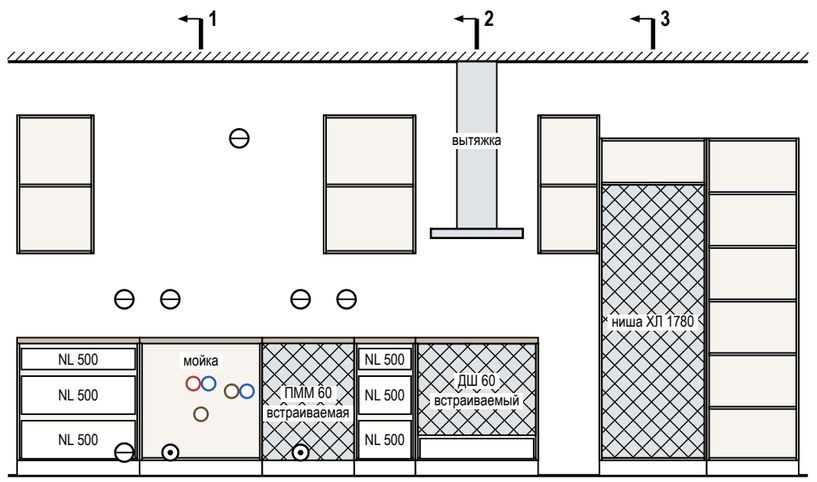


Разрез 1-1

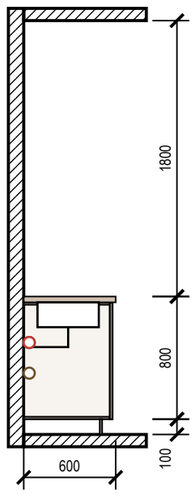

Разрез 2-2

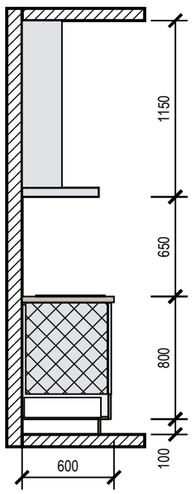

Разрез 3-3

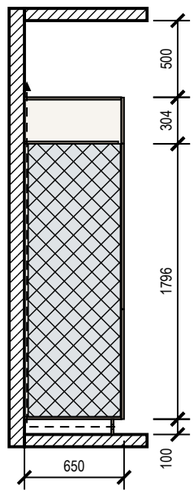

Условные обозначения

- фасад распашной: линии сходятся к стороне петель
- фасад ящика, карго
- встраиваемая техника
- столешница
- доборная планка
- деталь в разрезе
- К1 — марка изделия или модуля (на схеме расположения под ней — лист изделия)
- розетка на стене
- вывод кабеля к технике
- В1 — вывод воды В1 / Т3, канализации К1

Примечания

1. Размеры — в мм по чистовой отделке, вид из помещения; марки — как на плане расстановки. Перед раскроем — контрольный замер цеха после фартука и пола.
2. Корпуса — ЛДСП 16 мм, задняя стенка ХДФ 4 мм; фасады — МДФ, эмаль матовая 18 мм, цвет по колерной карте; столешница 38 мм, свес 20 мм; цоколь 100 мм.
3. Кромка: скрытые торцы 0,4 мм, видимые 2 мм. Номинальные зазоры: между фасадами 3 мм, фасад — столешница 3 мм, фасад — стена не менее 3 мм.
4. Ящики полного выдвижения и петли — с доводчиком; присадка по 32-й системе — выполняет цех.
5. Низ вытяжки — не ниже 650 мм над варочной панелью или по паспорту модели; короб воздуховода — до потолка.
6. Ниши техники (холодильник — ориентир 1780 мм) — по монтажным схемам выбранных моделей: решётка в цоколе и канал за пеналом холодильника, зазор за духовым шкафом, фасад ПММ на двери машины.

Допущения и предложения на листе

Основа листа: размеры и контуры этажей подобраны проектировщиком по составу помещений и площадям этажей с картинки 470 px (размеры на ней не читаются); обмер и исходный проект — задание (К-1); высоты: 1-й этаж 2800 мм, мансарда 2700 мм (горизонтальная часть) приняты; скаты кровли мансарды приняты по картинке: колено 1200 мм, уклон 45°, конёк вдоль длинной стороны; проект КР — задание (К-2); наружные стены 400 мм, перегородки 120 мм приняты (К-1); разрешённая мощность 15 кВт принята по типовым ТУ для частного дома (К-4); подрайон климата не задан — принят не северный (жилые от 2,5 м) (К-7).

См. лист открытых вопросов (лист 8, записи К-1, К-2, К-4, К-7).


1000 мм · печать 1:1

						ГД-2026-010-АИ	
						Дом 331 м²	
Изм.	Кол.уч	Лист	№ док.	Подп.	Дата	Общая площадь 270,67* м² · * размеры приняты, не замерены (реестр — л. 8–10, К-1)	
Разраб.		Кырлан А.С.			04.11.26	Дизайн-проект интерьера	Стадия: РП; Лист: 119; Листов: 216
Пров.							
ГИП							
						Кухня (пом. 1). Развёртка гарнитура	Кырлан Александр Сергеевич
Н. контр.						М 1:40	
Утв.							


Кухня (пом. 1). Монтажная схема

Кухня-столовая (пом. 1) · стена А · размеры в мм от чистых поверхностей, высоты — от чистого пола

Привязка выводов и крепление модулей

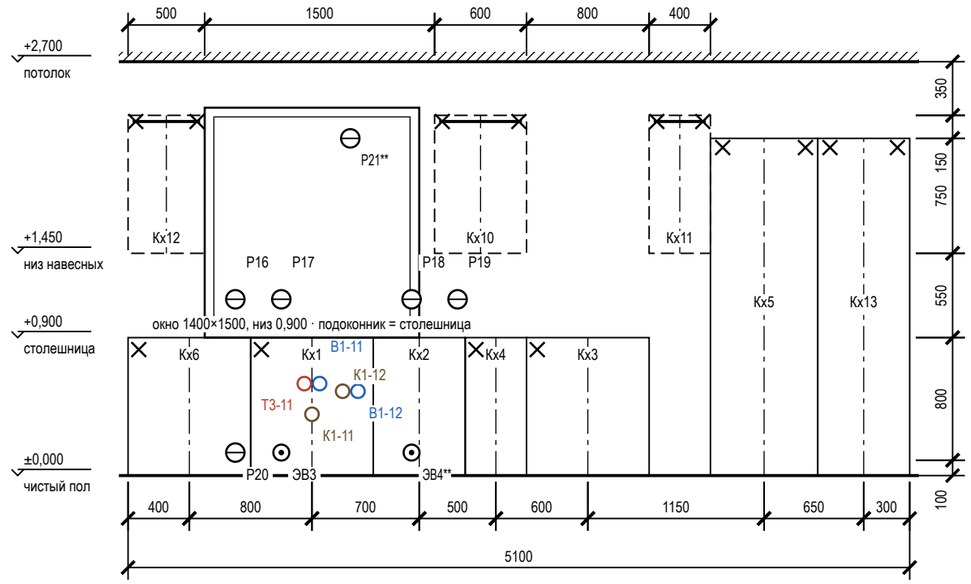

План столешницы

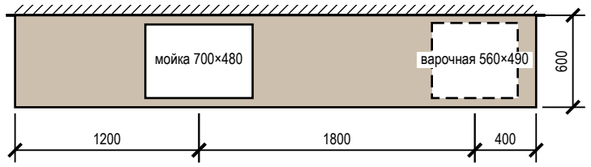

Привязка выводов к осям модулей

Код	Назначение	Модуль	От оси, мм	Н, мм	Размещение
P16	розетка ×2 — фартук: мелкая техника	Кх6	+300	1150	над столешницей (фартук)
P20	розетка — холодильник встроенный Кх5 (розетка в соседнем модуле)	Кх6	+300	150	в соседнем модуле, за ящиком
P17	розетка ×2 — фартук: мелкая техника	Кх1	−200	1150	над столешницей (фартук)
ЭВ3	вывод кабеля — варочная панель Кх3	Кх1	−200	150	в модуле мойки
T3-11	Т3 — межос. 100	Кх1	−50	600	в модуле мойки
K1-11	К1 Ø50 — мойка	Кх1	0	400	в модуле мойки
B1-11	В1 — межос. 100	Кх1	+50	600	в модуле мойки
K1-12	К1 Ø40 — слив ПММ в шкафу мойки	Кх1	+200	550	в модуле мойки
P21**	розетка — вытяжка над варочной панелью Кх3 (розетка за съёмной панелью)	Кх1	+250	2200	над столешницей (фартук)
B1-12	В1 — кран ПММ в шкафу мойки	Кх1	+300	550	в модуле мойки
P18	розетка ×2 — фартук: мелкая техника	Кх2	−50	1150	над столешницей (фартук)
ЭВ4**	вывод кабеля — духовой шкаф Кх3 (вывод в соседнем модуле)	Кх2	−50	150	за ПММ — перенести в соседний модуль
P19	розетка ×2 — фартук: мелкая техника	Кх2	+250	1150	над столешницей (фартук)

Зазоры под отделку

Поверхность	Отделка	Зазор, мм	Учесть
фартук	керамогранит	10	от чернового основания до корпуса навесных и столешницы
стены	окраска	5	под штукатурку и шпаклёвку за пеналом
пол	инженерная доска		цоколь — после укладки пола, опоры ±20 мм

Условные обозначения

- нижний модуль, пенал (контур)
- невидимый контур: навесной модуль, корпус под столешницей
- ось модуля (от неё — привязка вывода)
- анкер / уголок крепления к стене
- розетка на стене
- вывод кабеля к технике
- B1 — вывод воды В1 / Т3, канализации К1

Примечания

1. Окно над Кх6, Кх1, Кх2: низ проёма на 900 мм от пола, столешница на 900 мм, под окном мойка Кх1 — смеситель упирается в створку, открывающуюся внутрь; примыкание столешницы к откосу и подоконнику — до решения: решение по К-10; столешницу у окна не раскраивать до решения.
2. Выводы — по проекту электрики и ВК; привязка по горизонтали — от оси модуля (плюс — вправо по виду), по высоте — от чистого пола до оси вывода.
3. Пенал — уголки к стене 2 шт. сверху; нижние модули — стяжками между собой и уголком к стене; ряд выставить по уровню опорами цоколя.
4. Розетки над столешницей — не ниже 150 мм над ней и не за корпусом техники; розетка за ПММ, духовым шкафом и холодильником — только в соседнем модуле или в зоне цоколя с доступом.
5. Столешница — вырезы по шаблонам выбранных моделей мойки и варочной панели; торцы у стены — герметик, пристеночный плинтус.

Допущения и предложения на листе

Основа листа: размеры и контуры этажей подобраны проектировщиком по составу помещений и площадям этажей с картинки 470 px (размеры на ней не читаются); обмер и исходный проект — задание (К-1); высоты: 1-й этаж 2800 мм, мансарда 2700 мм (горизонтальная часть) приняты; скаты кровли мансарды приняты по картинке: колено 1200 мм, уклон 45°, конёк вдоль длинной стороны; проект КР — задание (К-2); наружные стены 400 мм, перегородки 120 мм приняты (К-1); разрешённая мощность 15 кВт принята по типовым ТУ для частного дома (К-4); подрайон климата не задан — принят не северный (жилые от 2,5 м) (К-7).

Знак «**» — предложение проектировщика, заказчиком не утверждено (согласовать с заказчиком): P21 — высота 2200 мм выше нормы 1 м (ПУЭ 6.6.30) по назначению: питание вытяжки над варочной панелью Кх3, розетка за съёмной панелью; ЭВ4 — по образцу: Добавлены выводы к вентиляторам: ЭВ4 (ВР1, ванная) и ЭВ5 (ВР3, санузел 2) — группа 3, высота 2389 мм, включение с основным светом, таймер выбега в вентиляторе; и коробки уравнивания потенциалов КУП1 (ванная) и КУП2 (санузел 2) — высота 300 мм, у входа, вне зон 0–2, проводник от шины PE щита ЩК …; сдвиг под раскладку плитки стены Б на 100 мм вдоль стены и на 14 мм выше — ось на шве или в центре плитки, привязка по таблице листа.

Открытые вопросы и конфликты по листу: К-10.

См. лист открытых вопросов (лист 8, записи К-1, К-2, К-4, К-7; лист 9, запись К-10).

1000 мм · печать 1:1

Изм.	Кол.уч	Лист	№ док.	Подп.	Дата
Разраб.		Кырлан А.С.			04.11.26
Пров.					
ГИП					
Н. контр.					
Утв.					

ГД-2026-010-АИ

Дом 331 м²

Общая площадь 270,67* м² · * размеры приняты, не замерены (реестр — л. 8–10, К-1)

Дизайн-проект интерьера

Стадия	Лист	Листов
РП	120	216

Кухня (пом. 1). Монтажная схема

М 1:40


Кырлан Александр Сергеевич

Остров Кх7 (пом. 1). Чертёж изделия

ПРЕДВАРИТЕЛЬНО · не для производства работ · открыто пунктов: 15 (реестр — л. 8–10)


Кухня-столовая (пом. 1) · остров с барной консолью из массива дуба, столешница — кварц · размеры в мм, отметки от чистого пола помещения

План (вид сверху)

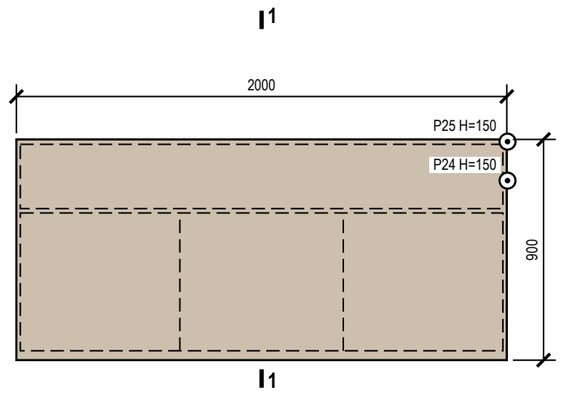


▲ рабочая сторона — северная (к стене А), проход 1100


Вид с рабочей стороны

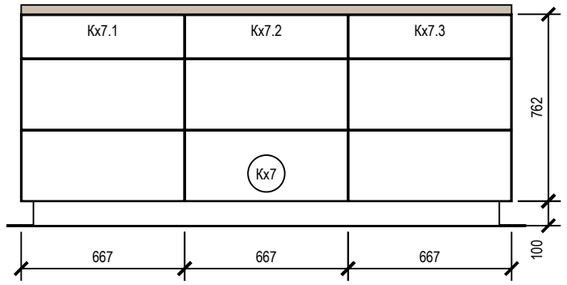


Вид без фасадов (наполнение, вывод)

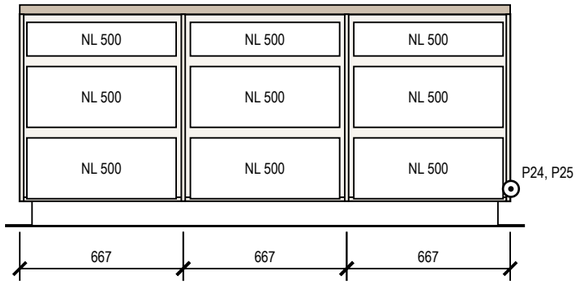

Разрез 1-1

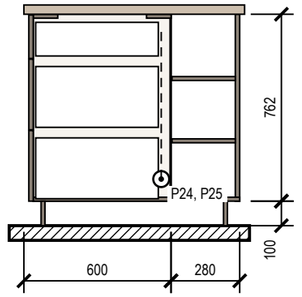

Вид с тыльной стороны

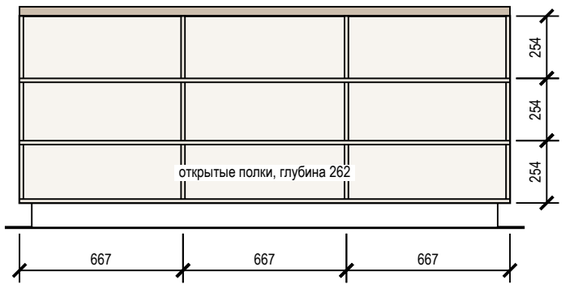

Условные обозначения

- фасад распашной: линии сходятся к стороне петель
- фасад ящика, карго
- столешница
- встраиваемая техника
- деталь в разрезе
- невидимый контур: навесной модуль, корпус под столешницей
- К1 — марка изделия или модуля (на схеме расположения под ней — лист изделия)
- вывод кабеля к технике

Примечания

1. Размеры — в мм по чистовому полу; перед раскроем — контрольный замер цеха после укладки пола. Остров крепится к полу (уголки в цоколе), выравнивается опорами ±20 мм.
2. Корпуса — ЛДСП 16 мм, задняя стенка ХДФ 4 мм; фасады — МДФ, эмаль матовая 18 мм; столешница 38 мм (материал — по наименованию изделия: столешница кварц), свес 20 мм по периметру; цоколь 100 мм с отступом 50 мм.
3. Кромка: скрытые торцы 0,4 мм, видимые 2 мм. Номинальные зазоры: между фасадами 3 мм, фасад — столешница 3 мм.
4. Рабочая сторона — северная (к стене А): проход 1100 мм; с тыла — открытые полки глубиной 262 мм. Членение и сторона — предложение мебельщика.
5. Питание: Р24 — торцевая панель острова Кх7: мелкая техника, H=150; Р25 — торцевая панель острова Кх7: мелкая техника, H=150; кабель — внутри модуля до панели, доступ через съёмный цоколь.

Спецификация изделия Кх7

Поз.	Наименование	Тип, размер	Кол.
Кх7.1	модуль с ящиками	667×900×900	1
Кх7.2	модуль с ящиками	667×900×900	1
Кх7.3	модуль с ящиками	667×900×900	1
	Направляющие полного выдвижения с доводчиком NL 500	пара	9
	Ручка-профиль	латунь матовая	9
	Опора кухонная регулируемая 100–120 мм	+ клипса цоколя	18
	Уголок крепления острова к полу	стальной, в цоколе	4
	Полкодержатель с фиксацией	ø5 мм	24

Допущения и предложения на листе

Основа листа: размеры и контуры этажей подобраны проектировщиком по составу помещений и площадям этажей с картинки 470 px (размеры на ней не читаются); обмер и исходный проект — задание (К-1); высоты: 1-й этаж 2800 мм, мансарда 2700 мм (горизонтальная часть) приняты; скаты кровли мансарды приняты по картинке: колено 1200 мм, уклон 45°, конёк вдоль длинной стороны; проект КР — задание (К-2); наружные стены 400 мм, перегородки 120 мм приняты (К-1); разрешённая мощность 15 кВт принята по типовым ТУ для частного дома (К-4); подрайон климата не задан — принят не северный (жилые от 2,5 м) (К-7).

См. лист открытых вопросов (лист 8, записи К-1, К-2, К-4, К-7).

1000 мм · печать 1:1

Изм.	Кол.уч	Лист	№ док.	Подп.	Дата
Разраб.		Кырлан А.С.			04.11.26
Пров.					
ГИП					
Н. контр.					
Утв.					

ГД-2026-010-АИ

Дом 331 м²

Общая площадь 270,67* м² · * размеры приняты, не замерены (реестр — л. 8–10, К-1)

Дизайн-проект интерьера

Стадия	Лист	Листов
РП	121	216

Остров Кх7 (пом. 1). Чертёж изделия

М 1:25

Кырлан Александр Сергеевич


выпуск 04.11.2026 № 2a77323a49 · стр. 124 из 221

Шкафы. Монтажная схема. Лист 1 из 2


крепление к стене, установочные размеры, зазоры под отделку · размеры в мм, отметки в м от ±0,000 (чистый пол 1-го этажа)

ПРЕДВАРИТЕЛЬНО · не для производства работ · открыто пунктов: 15 (реестр — л. 8–10)


Система хранения Кт1 (пом. 4)

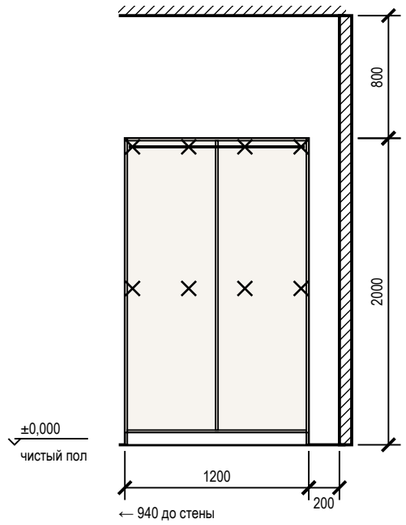


Система хранения Кл1 (пом. 7)

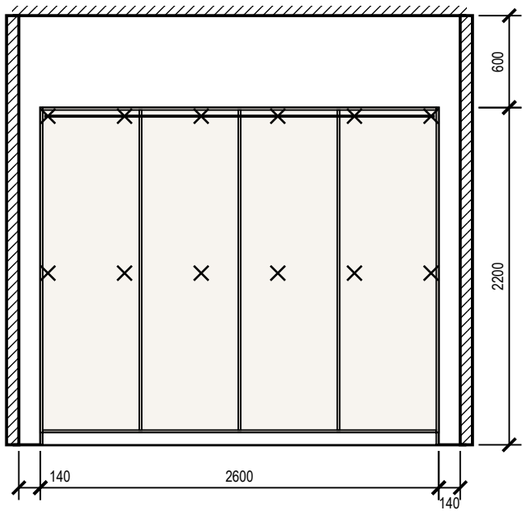

Шкаф-купе Пх1 (пом. 8)

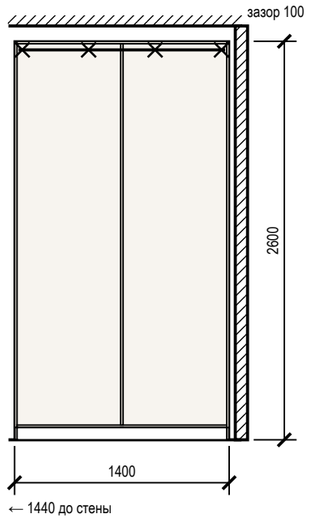

Система хранения Гр1 (пом. 10)

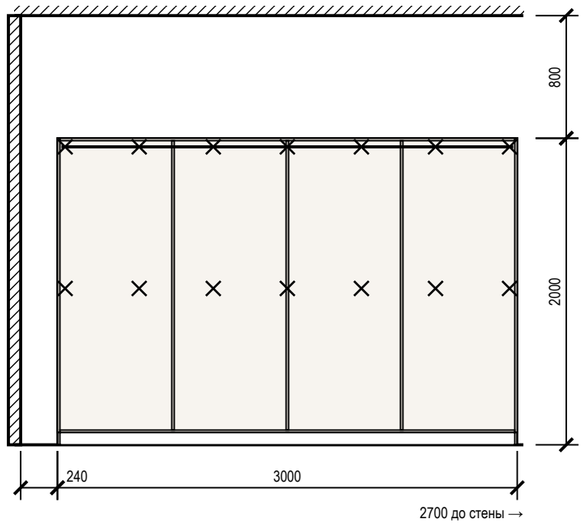

Крепление и зазоры под отделку (изделия листа 1)

Марка	Помещение, стена	Основание	Отделка стены	Зазор, мм	Крепёж по планке	От опрокидывания
Кт1	Котельная (4), стена Г	по основанию — см. таблицу крепежа	окраска	5	анкер 8 шт. (2 ряда)	уголки 2 шт.
Кл1	Кладовая (7), стена В	по основанию — см. таблицу крепежа	окраска	5	анкер 12 шт. (2 ряда)	уголки 2 шт.
Пх1	Прихожая (8), стена А	по основанию — см. таблицу крепежа	окраска	5	анкер 4 шт., шаг 433	уголки 2 шт.
Гр1	Гараж (10), стена А	по основанию — см. таблицу крепежа	окраска	5	анкер 14 шт. (2 ряда)	уголки 2 шт.

Крепёж по основанию стены

Основание стены	Крепёж
бетон, ж/б	анкер-шуруп 7,5×72 или дюбель 8×60 с шурупом 5×70
кирпич полнотелый	дюбель 8×80 с шурупом 5×90
газобетон, пазогребень	дюбель для газобетона 10×100 или химический анкер
гипсокартон	закладная до обшивки (брус 40×80 или фанера 18 мм), саморез в закладную

Условные обозначения

- анкер / уголок крепления к стене
- корпус и полки ЛДСП (вид на стену)
- компенсатор — короб до потолка

Примечания

1. Установочные размеры — от чистого пола и чистых стен; перед установкой контрольный замер после отделки.
2. Порядок: корпус выставить по уровню опорами цоколя → закрепить к стене по задней планке → навесить двери и фасады, отрегулировать зазоры → подогнать и закрепить компенсатор.
3. Анкеры — с шагом не более 500 мм, не ближе 50 мм от края планки; на ГКЛ только в закладную, установленную до обшивки.
4. Скрытые коммуникации под анкеры проверить детектором; трассы электрики по плану розеток.
5. Монтажная схема на 2 листах, лист 1 из 2; продолжение — на следующем листе схемы. Условные обозначения, таблица крепежа по основанию и примечания повторены на каждом листе.

Допущения и предложения на листе

Основа листа: размеры и контуры этажей подобраны проектировщиком по составу помещений и площадям этажей с картинки 470 px (размеры на ней не читаются); обмер и исходный проект — задание (К-1); высоты: 1-й этаж 2800 мм, мансарда 2700 мм (горизонтальная часть) приняты; скаты кровли мансарды приняты по картинке: колено 1200 мм, уклон 45°, конёк вдоль длинной стороны; проект КР — задание (К-2); наружные стены 400 мм, перегородки 120 мм приняты (К-1); разрешённая мощность 15 кВт принята по типовым ТУ для частного дома (К-4); подрайон климата не задан — принят не северный (жилые от 2,5 м) (К-7).
См. лист открытых вопросов (лист 8, записи К-1, К-2, К-4, К-7).

1000 мм · печать 1:1

Изм.	Кол.уч	Лист	№ док.	Подп.	Дата
Разраб.		Кырлан А.С.			04.11.26
Пров.					
ГИП					
Н. контр.					
Утв.					

ГД-2026-010-АИ

Дом 331 м²

Общая площадь 270,67* м² · * размеры приняты, не замерены (реестр — л. 8–10, К-1)

Дизайн-проект интерьера

Стадия	Лист	Листов
РП	122	216

Шкафы. Монтажная схема. Лист 1 из 2

М 1:40

Кырлан Александр Сергеевич


выпуск 04.11.2026 № 2a77323a49 · стр. 125 из 221

Шкафы. Монтажная схема. Лист 2 из 2


крепление к стене, установочные размеры, зазоры под отделку · размеры в мм, отметки в м от ±0,000 (чистый пол 1-го этажа)

ПРЕДВАРИТЕЛЬНО · не для производства работ · открыто пунктов: 15 (реестр — л. 8–10)


Система хранения Гм2 (пом. 14)

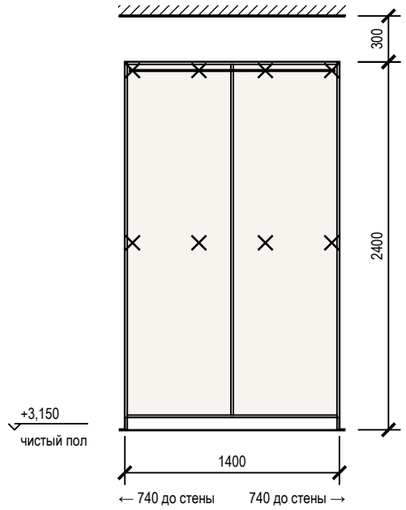


Шкаф распашной С3 (пом. 16)

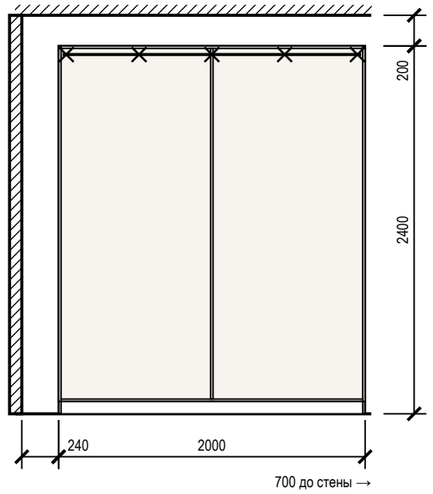


Система хранения Сп3 (пом. 17)

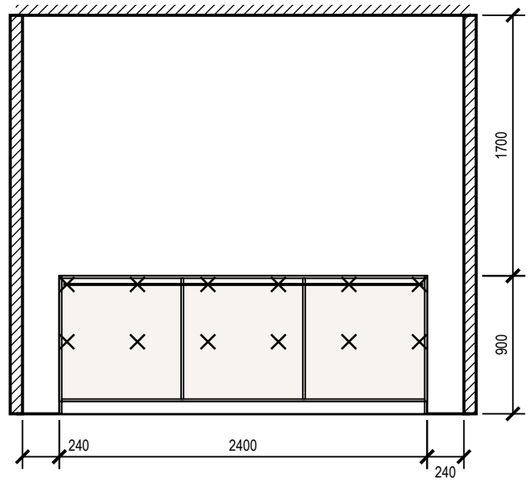

Шкаф распашной Дт3 (пом. 18)

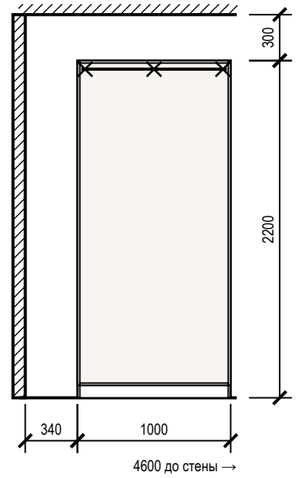

Шкаф распашной Дт6 пом. 19

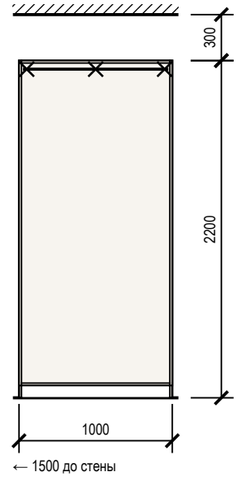

Крепление и зазоры под отделку (изделия листа 2)

Марка	Помещение, стена	Основание	Отделка стены	Зазор, мм	Крепёж по планке	От опрокидывания
Гм2	Гардеробная мастер (14), стена В	по основанию — см. таблицу крепежа	окраска	5	анкер 8 шт. (2 ряда)	уголки 2 шт.
С3	Спальня 2 (16), стена А	по основанию — см. таблицу крепежа	окраска	5	анкер 5 шт., шаг 475	уголки 2 шт.
Сп3	Холл мансарды (17), стена В	по основанию — см. таблицу крепежа	окраска	5	анкер 12 шт. (2 ряда)	уголки 2 шт.
Дт3	Спальня 3 (18), стена В	по основанию — см. таблицу крепежа	окраска	5	анкер 3 шт., шаг 450	уголки 2 шт.
Дт6	Спальня 4 (19), стена А	по основанию — см. таблицу крепежа	окраска	5	анкер 3 шт., шаг 450	уголки 2 шт.

Крепёж по основанию стены

Основание стены	Крепёж
бетон, ж/б	анкер-шуруп 7,5×72 или дюбель 8×60 с шурупом 5×70
кирпич полнотелый	дюбель 8×80 с шурупом 5×90
газобетон, пазогребень	дюбель для газобетона 10×100 или химический анкер
гипсокартон	закладная до обшивки (брус 40×80 или фанера 18 мм), саморез в закладную

Условные обозначения

- анкер / уголок крепления к стене
- корпус и полки ЛДСП (вид на стену)
- компенсатор — короб до потолка

Примечания

1. Установочные размеры — от чистого пола и чистых стен; перед установкой контрольный замер после отделки.
2. Порядок: корпус выставить по уровню опорами цоколя → закрепить к стене по задней планке → навесить двери и фасады, отрегулировать зазоры → подогнать и закрепить компенсатор.
3. Анкеры — с шагом не более 500 мм, не ближе 50 мм от края планки; на ГКЛ только в закладную, установленную до обшивки.
4. Скрытые коммуникации под анкеры проверить детектором; трассы электрики по плану розеток.
5. Монтажная схема на 2 листах, лист 2 из 2. Условные обозначения, таблица крепежа по основанию и примечания повторены на каждом листе.

Допущения и предложения на листе

Основа листа: размеры и контуры этажей подобраны проектировщиком по составу помещений и площадям этажей с картинки 470 px (размеры на ней не читаются); обмер и исходный проект — задание (К-1); высоты: 1-й этаж 2800 мм, мансарда 2700 мм (горизонтальная часть) приняты; скаты кровли мансарды приняты по картинке: колено 1200 мм, уклон 45°, конёк вдоль длинной стороны; проект КР — задание (К-2); наружные стены 400 мм, перегородки 120 мм приняты (К-1); разрешённая мощность 15 кВт принята по типовым ТУ для частного дома (К-4); подрайон климата не задан — принят не северный (жилые от 2,5 м) (К-7).

Знак «*» — принято, не замерено и не подтверждено (замерить на объекте): К-2: отметка чистого пола этажа «Мансарда» +3,150 — принята без источника, все отметки мансарды считаются от неё.

См. лист открытых вопросов (лист 8, записи К-1, К-2, К-4, К-7).

1000 мм · печать 1:1

Изм.	Кол.уч	Лист	№ док.	Подп.	Дата
Разраб.		Кырлан А.С.			04.11.26
Пров.					
ГИП					
Н. контр.					
Утв.					

ГД-2026-010-АИ

Дом 331 м²

Общая площадь 270,67* м² · * размеры приняты, не замерены (реестр — л. 8–10, К-1)

Дизайн-проект интерьера

Стадия	Лист	Листов
РП	123	216

Шкафы. Монтажная схема. Лист 2 из 2

М 1:40

Кырлан Александр Сергеевич

выпуск 04.11.2026 № 2a77323a49 · стр. 126 из 221

Ведомости изделий, техники и фурнитуры

встроенная мебель и кухонный гарнитур · размеры в мм

Ведомость изделий

Марка	Наименование	Пом.	Ш×Г×В, мм	Корпус	Фасад	Кромка, мм	Кол.
Кт1	Система хранения	4	1200×400×2000	ЛДСП 16	без фасадов	0,4 / 2	1
Кл1	Система хранения	7	2600×500×2200	ЛДСП 16	без фасадов	0,4 / 2	1
Пх1	Шкаф-купе	8	1400×600×2600	ЛДСП 16	ЛДСП 10 мм в алюминиевом профиле	0,4 / 2	1
Гр1	Система хранения	10	3000×500×2000	ЛДСП 16	без фасадов	0,4 / 2	1
Гм2	Система хранения	14	1400×500×2400	ЛДСП 16	без фасадов	0,4 / 2	1
С3	Шкаф распашной	16	2000×600×2400	ЛДСП 16	МДФ 18 мм, эмаль матовая	0,4 / 2	1
Сп3	Система хранения	17	2400×350×900	ЛДСП 16	без фасадов	0,4 / 2	1
Дт3	Шкаф распашной	18	1000×600×2200	ЛДСП 16	МДФ 18 мм, эмаль матовая	0,4 / 2	1
Дт6	Шкаф распашной	19	1000×600×2200	ЛДСП 16	МДФ 18 мм, эмаль матовая	0,4 / 2	1
Кх6	Модуль нижний: ящики	1	800×600×900	ЛДСП 16	МДФ 18 мм, эмаль матовая	0,4 / 2	1
Кх12	Модуль навесной: полки	1	500×350×900	ЛДСП 16	МДФ 18 мм, эмаль матовая	0,4 / 2	1
Кх1	Модуль нижний: мойка	1	800×600×900	ЛДСП 16	МДФ 18 мм, эмаль матовая	0,4 / 2	1
Кх2	Модуль под ПММ 60: без корпуса, фасад на дверь машины	1	600×600×900	без корпуса	МДФ 18 мм, эмаль матовая — на дверь машины (навеска из её комплекта), цоколь		1
Кх10	Модуль навесной: полки	1	600×350×900	ЛДСП 16	МДФ 18 мм, эмаль матовая	0,4 / 2	1
Кх4	Модуль нижний: ящики	1	400×600×900	ЛДСП 16	МДФ 18 мм, эмаль матовая	0,4 / 2	1
Кх3	Модуль нижний: духовой шкаф, варочная	1	800×600×900	ЛДСП 16	МДФ 18 мм, эмаль матовая	0,4 / 2	1
Кх11	Модуль навесной: полки	1	400×350×900	ЛДСП 16	МДФ 18 мм, эмаль матовая	0,4 / 2	1
Кх5	Пенал: холодильник встр.	1	700×650×2200	ЛДСП 16	МДФ 18 мм, эмаль матовая	0,4 / 2	1
Кх13	Пенал: полки	1	600×600×2200	ЛДСП 16	МДФ 18 мм, эмаль матовая	0,4 / 2	1
Кх7	Остров (Кх7.1, Кх7.2, Кх7.3)	1	2000×900×900	ЛДСП 16	МДФ 18 мм, эмаль матовая	0,4 / 2	1

Ведомость встраиваемой техники

Поз.	Прибор	Ниша, вырез, мм	Вентиляция	Питание	Схема
Кх1	Мойка врезная / подстольная с сифоном	вырез по шаблону, ориентир 700 × 480		смеситель — выводы ВК	по модели
Кх2	Посудомоечная машина встраиваемая, 60 см	ниша 600 × 862 (от пола до низа столешницы)	зазор в цоколе, по схеме	питание: точка ЭОМ не задана — вывод под прибор не делать до задания	по модели
Кх3	Духовой шкаф встраиваемый, 60 см	ниша 560 × 600, глубина ≥ 550	зазор за шкафом, вырез в задней стенке	питание: точка ЭОМ не задана — вывод под прибор не делать до задания	по модели
Кх3	Варочная панель индукционная, 60 см	вырез в столешнице 560 × 490		питание: точка ЭОМ не задана — вывод под прибор не делать до задания	по модели
Кх5	Холодильник встраиваемый, ниша 1780	ниша 1780 × 560 × 550	решётка в цоколе, канал за корпусом, выход сверху	питание: точка ЭОМ не задана — вывод под прибор не делать до задания	по модели
Кх3	Вытяжка настенная, 60 см	низ ≥ 650 над панелью	воздуховод к вентканалу, короб до потолка	вывод кабеля в коробе	по модели

Допущения и предложения на листе. Основа листа: размеры и контуры этажей подобраны проектировщиком по составу помещений и площадям этажей с картинки 470 px (размеры на ней не читаются); обмер и исходный проект — задание (К-1); высоты: 1-й этаж 2800 мм, мансарда 2700 мм (горизонтальная часть) приняты; скаты кровли мансарды приняты по картинке: колено 1200 мм, уклон 45°, конёк вдоль длинной стороны; проект КР — задание (К-2); наружные стены 400 мм, перегородки 120 мм приняты (К-1); разрешённая мощность 15 кВт принята по типовым ТУ для частного дома (К-4); подрайон климата не задан — принят не северный (жилые от 2,5 м) (К-7). См. лист открытых вопросов (лист 8, записи К-1, К-2, К-4, К-7; лист 10, записи ИЗ-2, Кф-1); по листу — Кф-1, ИЗ-2.

Ведомость фурнитуры

№	Фурнитура	Тип, размер	Изделия	Кол.
1	Штанга выдвижная торцевая	L по глубине	Кт1, Кл1, Гр1, Гм2	6
2	Полкодержатель с фиксацией	ø5 мм	Кт1, Кл1, Пх1, Гр1, Гм2, С3, Сп3, Дт3, Дт6, Кх12, Кх10, Кх11, Кх5, Кх13, Кх7	252
3	Опора регулируемая с цоколем на клипсах	ход 20 мм	Кт1, Кл1, Пх1, Гр1, Гм2, С3, Сп3, Дт3, Дт6	66
4	Анкер по основанию стены	по таблице крепежа	Кт1, Кл1, Пх1, Гр1, Гм2, С3, Сп3, Дт3, Дт6, Кх12, Кх10, Кх11	75
5	Уголок крепления к стене от опрокидывания	стальной	Кт1, Кл1, Пх1, Гр1, Гм2, С3, Сп3, Дт3, Дт6, Кх5, Кх13	22
6	Система дверей купе: профиль, направляющие, ролики	на 2 двери	Пх1	1
7	Ручка-профиль вертикальная	в цвет профиля	Пх1	2
8	Штанга овальная 30×15, L = 676	+ 2 держателя	Пх1	1
9	Полка для обуви выдвижная наклонная	ширина 676	Пх1	3
10	Петля накладная 110° с доводчиком	чашка 35 мм	С3, Дт3, Дт6, Кх12, Кх1, Кх10, Кх11, Кх5, Кх13	72
11	Штанга овальная 30×15, L = 976	+ 2 держателя	С3	1
12	Штанга овальная 30×15, L = 968	+ 2 держателя	Дт3, Дт6	2
13	Направляющие полного выдвижения с доводчиком NL 500	пара	Кх6, Кх4, Кх3, Кх7	16
14	Ручка-профиль	латунь матовая	Кх6, Кх12, Кх1, Кх2, Кх10, Кх4, Кх3, Кх11, Кх5, Кх13, Кх7	28
15	Опора кухонная регулируемая 100–120 мм	+ клипса цоколя	Кх6, Кх1, Кх4, Кх3, Кх5, Кх13, Кх7	50
16	Навес регулируемый для навесного шкафа	пара на секцию	Кх12, Кх10, Кх11	3
17	Шина монтажная	L = 440	Кх12	1
18	Комплект навески фасада ПММ	из поставки машины	Кх2	1
19	Шина монтажная	L = 540	Кх10	1
20	Шина монтажная	L = 340	Кх11	1
21	Уголок крепления острова к полу	стальной, в цоколе	Кх7	4

Примечания

1. Модели техники выбирает заказчик до изготовления мебели; ниши, вырезы и вентиляция — по монтажной схеме выбранной модели (условие гарантии), её номер вносится в ведомость.
2. Количество фурнитуры — по чертежам изделий; запас крепежа 5 %. Аналоги — по характеристикам (доводчик, нагрузка, ход).
3. Цвет корпусов, фасадов и профилей — по колерной карте проекта. Кромка — скрытые / видимые торцы, мм.

Изм.	Кол.уч	Лист	№ док.	Подп.	Дата

ГД-2026-010-АИ

Дом 331 м²

Общая площадь 270,67* м² · * размеры приняты, не замерены (реестр — л. 8–10, К-1)

Разраб.	Кырлан А.С.		04.11.26
Пров.			
ГИП			
Н. контр.			
Утв.			

Дизайн-проект интерьера

Стадия	Лист	Листов
РП	124	216

Ведомости изделий, техники и фурнитуры

М б/м

Кырлан Александр Сергеевич

выпуск 04.11.2026 № 2a77323a49 · стр. 127 из 221

04

Развёртки и узлы



Кырлан Александр Сергеевич

выпуск 04.11.2026 № 2a77323a49 · стр. 128 из 221

Реестр марок отделки и позиций альбома

Реестр марок отделки (О ↔ позиции колерной карты) и марки позиций по видам

Допущения и предложения на листе. Знак «*» принято (замерить): пол пом. 11, 12. Знак «**» предложено (согласовать): плинтус пом. 1, 2, 4–14, 16, 17, фартук пом. 1, пол пом. 3, 10, 15, 20, акцент пом. 5. См. лист открытых вопросов (листы 8–10).

Реестр марок отделки альбома

Марка	Поверхность	Материал, изделие	Цвет, код	Помещения	Колер. карта
О1	стены	окраска, Tikkurila Luja 7, шелковисто-матовая, подготовка К3	NCS S 0804-Y30R «S 0804-Y30R»	1, 11, 12	К1
О2	фартук	керамогранит, аналог: керамогранит матовый, тон F497, затирка CG2WA	#F1F1EC «тон Paper F497»	1	КМ2
О3	плинтус	плинтус МДФ, h 80 мм, аналог: плинтус МДФ под окраску 80×16 мм, полуглянцевая	NCS S 0804-Y30R «S 0804-Y30R»	1, 5	К3
О4	потолок	окраска, Tikkurila Luja 7, матовая, подготовка Q3	NCS S 0804-Y30R «S 0804-Y30R»	1, 11, 12	К2
О5	пол	инженерная доска, Coswick Вековые традиции, 2100×127 мм, 1167-4250		1, 2, 5, 6, 7, 13, 14, 16, 17, 18, 19	КМ1
О6	стены	окраска, Farrow & Ball Modern Emulsion, матовая, подготовка Q3	Farrow & Ball No. 226 «Joa's White»	2, 4, 6, 8, 9, 10, 13, 16, 17, 18, 19	К4
О7	акцентная стена	окраска, Farrow & Ball Modern Emulsion, матовая, подготовка Q3	Farrow & Ball No. 298 «Bancha»	2	К5
О8	плинтус	плинтус МДФ, h 80 мм, аналог: плинтус МДФ под покраску 80×16	Farrow & Ball No. 226 «Joa's White»	2, 4, 6, 8, 9, 13, 16, 17	К7
О9	потолок	окраска, Little Greene Absolute Matt, глубокоматовая, подготовка Q3	Little Greene No. 105 «Slaked Lime»	2, 4, 6, 7, 8, 9, 10, 13, 14, 16, 17, 18, 19	К6
О10	стены	облицовка плиткой, Atlas Concorde Marvel Travertine, 600×1200×9 мм, A8UZ, затирка CG2WA	Atlas Concorde A8UZ «Marvel Travertine»	3, 15, 20	КМ3
О11	потолок	окраска, Little Greene Intelligent Bathroom, матовая, подготовка Q3	Little Greene No. 105 «Slaked Lime»	3, 15, 20	К8
О12	пол	керамогранит, 600×600×9 мм, аналог: керамогранит ректифицированный под травертин, матовый, затирка CG2WA		3, 15, 20	КМ4
О13	пол	керамогранит, Atlas Concorde Marvel Travertine, 600×1200×9 мм, A8UZ, затирка CG2WA	Atlas Concorde A8UZ «Marvel Travertine»	4, 8, 9	КМ5
О14	стены	окраска, Tikkurila Optiva 5 Matt, матовая, подготовка К3	NCS S 0804-Y30R «S 0804-Y30R»	5	К9
О15	акцентная стена	окраска, Farrow & Ball Modern Emulsion, аналог: интерьерная краска, класс 2 по EN 13300, глубокоматовая/матовая, база C, матовая, подготовка К3	Farrow & Ball No. 93 «Studio Green — почти чёрный зелёный»	5	К10
О16	потолок	окраска, Tikkurila Anti-Reflex 2, глубокоматовая, подготовка Q3	NCS S 0804-Y30R «S 0804-Y30R»	5	К11
О17	стены	окраска, Little Greene Intelligent Matt, матовая, подготовка Q3	Little Greene No. 105 «Slaked Lime»	7, 14	К12
О18	плинтус	плинтус МДФ, h 80 мм, аналог: плинтус МДФ под покраску 80×16	Little Greene No. 105 «Slaked Lime»	7, 14	К13
О19	плинтус	плинтус ПВХ, h 100 мм, аналог: плинтус ПВХ влагостойкий 100 мм, серый		10	КМ7
О20	пол	ероху, аналог: наливной полимерный пол (эпоксидный), с кварцевой посыпкой, 3 мм		10	КМ6
О21	плинтус	керамогранит, аналог: плинтус из керамогранита пола, подрезка 80 мм, верхняя кромка с запилом 45°	#B8AFA5 «тон Claystone V486»	11, 12	КМ8

Реестр марок отделки альбома (продолжение)

Марка	Поверхность	Материал, изделие	Цвет, код	Помещения	Колер. карта
О22	пол	керамогранит, Atlas Concorde Marvel Travertine, 600×1200×10 мм, A8UZ, затирка CG2WA	#B8AFA5 «тон Claystone V486»	11, 12	КМ5
О23	акцентная стена	окраска, Tikkurila Optiva 5 Matt, матовая, подготовка Q3	NCS S 7020-G10Y «Хвойный тёмно-зелёный»	13	К14
О24	акцентная стена	окраска, Farrow & Ball Modern Emulsion, матовая, подготовка Q3	Farrow & Ball No. 64 «Red Earth»	16	К15
О25	акцентная стена	окраска, Tikkurila Optiva 5 Matt, матовая, подготовка Q3	NCS S 3020-G30Y «S 3020-G30Y»	18	К16
О26	плинтус	плинтус МДФ, Orac Decor Contour (Luxxus), h 69 мм, SX165	Farrow & Ball No. 226 «Joa's White»	18, 19	К17
О27	акцентная стена	окраска, Tikkurila Optiva 5 Matt, матовая, подготовка Q3	NCS S 3040-Y70R «S 3040-Y70R»	19	К18

Марки позиций альбома по видам

Префикс	Что обозначает, позиции	Листы
В, Д, Д-вх	двери: В-1, Д-1–Д-14, Д-вх	19–27
Пр	проёмы без полотна (порталы): Пр-1–Пр-3	19–27
ОК	окна: ОК-1–ОК-7	19–27
Вр, Гм, Гр, Гс, Дт, Кб, Кл, Кт, Кх, М, Пх, С, Сп	мебель и оборудование: Вр1, Вр2, Вр4–Вр6, Гм1, Гм2, Гр1–Гр6, Гс1–Гс6, Дт1–Дт6, Кб1–Кб4, Кл1, Кт1, Кх1–Кх8, Кх10–Кх13, М1–М5, Пх1, Пх2, С1–С3, Сп1–Сп4	28–36
Сд, См, Сн	сантехнические приборы: Сд1–Сд4, См1–См4, Сн1**, Сн2–Сн4	56–70
ДК	декор (картины, зеркала, растения): ДК1–ДК13, ДК21–ДК28, ДК30, ДК31	1, 99–107
Т	текстиль (шторы, ковры): Т1–Т37, Т40, Т41	1, 99–107
Р	розетки: Р1–Р6, Р7**, Р8**, Р9–Р11, Р12**, Р13–Р20, Р21**, Р22–Р26, Р33**, Р34, Р35, Р36**, Р37**, Р38**, Р39, Р40**, Р41–Р47, Р48**, Р49**, Р50–Р52, Р53**, Р54–Р59, Р60**, Р61–Р65, Р66**, Р67, Р68	37–51
ЭВ	выводы кабеля: ЭВ3, ЭВ4**, ЭВ5**, ЭВ6**, ЭВ7**, ЭВ8**, ЭВ9**	37–51
S	выключатели: S1, S2**, S3–S8, S10–S34	37–51
Св	светильники: Св1–Св14, Св15**, Св16–Св29, Св30**, Св31–Св40, Св50, Св51, Св52**, Св53–Св58, Св59**, Св60**, Св61–Св74, Св75**, Св76–Св104	37–51
БП	блоки питания LED: БП1–БП9	37–51

Изм.	Кол.уч	Лист	№ док.	Подп.	Дата
Разраб.		Кырлан А.С.			04.11.26
Пров.					
ГИП					
Н. контр.					
Утв.					

ГД-2026-010-АИ

Дом 331 м²

Общая площадь 270,67* м² · * размеры приняты, не замерены (реестр — л. 8–10, К-1)

Дизайн-проект интерьера

Стадия	Лист	Листов
РП	125	216

Реестр марок отделки и позиций альбома

М б/м

Кырлан Александр Сергеевич

выпуск 04.11.2026 № 2a77323a49 · стр. 129 из 221

Реестр марок отделки и позиций альбома (продолжение)

Реестр марок отделки (О ↔ позиции колерной карты) и марки позиций по видам

Марки позиций альбома по видам (продолжение)

Префикс	Что обозначает, позиции	Листы
ИП	извещатели: ИП1, ИП2, ИП3**, ИП4, ИП6**, ИП7, ИП8, ИП9**, ИП10, ИП11, ИП12**	37–51
ТВ	розетки ТВ: ТВ1–ТВ5	37–51
LAN	розетки компьютерные: LAN1–LAN6	37–51
КУП	электроустановочные изделия: КУП1**, КУП2**, КУП3**	37–51
ЩК, ЩС**	щиты: ЩК, ЩС**	37–51
ДФ	домофон: ДФ1	37–51
АР	точки доступа Wi-Fi: АР1**	37–51
Ст В1, Ст К1, Ст К1-2 (кухня), Ст Т3	стояки (системы В1, Т3, К1): Ст В1-1, Ст В1-2, Ст В1-3, Ст К1-1, Ст К1-2 (кухня), Ст К1-3, Ст Т3-1, Ст Т3-2, Ст Т3-3	56–70
О	марки отделки (реестр альбома): О1–О27	2–7, 125–206
К, КМ	позиции колерной карты: К1–К18, КМ1–КМ8	95–98
РО	радиаторы отопления: РО-1**, РО-2**, РО-3**, РО-4**, РО-5**, РО-6**, РО-7**, РО-8**, РО-9**, РО-10**, РО-11**	52–55

Примечания

1. Марка отделки О — одна на весь альбом: одна и та же отделка (материал, изделие, цвет, формат) на всех листах имеет одну марку; на развёртках и планах стоят марки этого реестра.
2. Столбец «Колер. карта» — позиции колерной карты (лист 95): К — окраска по коду цвета, КМ — материал без кода цвета; «Помещения» — номера по экспликации; количества — по ведомости отделки помещений (лист 91).
3. Марки позиций: один префикс — один вид позиций на весь альбом (двери Д, окна ОК, мебель М, сантехприборы П, декор ДК, текстиль Т, колерная карта К и КМ, радиаторы РО, розетки Р, выключатели S, светильники Св; стояки — «Ст» и система, например «Ст К1-1»). Совпадение префиксов у разных видов — замечание к исходным данным, при выпуске исправляется в модели.

Допущения и предложения на листе

Основа листа: размеры и контуры этажей подобраны проектировщиком по составу помещений и площадям этажей с картинки 470 px (размеры на ней не читаются); обмер и исходный проект — задание (К-1); высоты: 1-й этаж 2800 мм, мансарда 2700 мм (горизонтальная часть) приняты; скаты кровли мансарды приняты по картинке: колено 1200 мм, уклон 45°, конёк вдоль длинной стороны; проект КР — задание (К-2); наружные стены 400 мм, перегородки 120 мм приняты (К-1); разрешённая мощность 15 кВт принята по типовым ТУ для частного дома (К-4); подрайон климата не задан — принят не северный (жилые от 2,5 м) (К-7).

Знак «*» — принято, не замерено и не подтверждено (замерить на объекте): К-13: пол пом. 11, 12 — отметка верха плиты −0,170 принята по пирогу (плита веранды и крыльца своя, ниже плиты дома) — подтвердить по проекту КР или обмером (К-13).

Знак «**» — предложение проектировщика, заказчиком не утверждено (согласовать с заказчиком): КУП1 — по образцу: Добавлены выводы к вентиляторам: ЭВ4 (ВР1, ванная) и ЭВ5 (ВР3, санузел 2) — группа 3, высота 2389 мм, включение с основным светом, таймер выбега в вентиляторе; и коробки уравнивания потенциалов КУП1 (ванная) и КУП2 (санузел 2) — высота 300 мм, у входа, вне зон 0–2, проводник от шины PE щита ЩК …; сдвиг под раскладку плитки стены В на 131 мм вдоль стены — ось на шве или в центре плитки, привязка по таблице листа; ИП6, ИП3, ИП9 — дымовой автономный вместо теплового образца: жилой дом — автономные дымовые в путях эвакуации (СП 486, пункт сверить по действующей редакции); ИП12 — жилой дом — автономные дымовые извещатели в жилых комнатах и путях эвакуации (СП 486, пункт сверить по действующей редакции); место — центр помещения, не ближе 500 мм к светильнику; КУП3 — по образцу: Добавлены выводы к вентиляторам: ЭВ4 (ВР1, ванная) и ЭВ5 (ВР3, санузел 2) — группа 3, высота 2389 мм, включение с основным светом, таймер выбега в вентиляторе; и коробки уравнивания потенциалов КУП3 (ванная) и КУП2 (санузел 2) — высота 300 мм, у входа, вне зон 0–2, проводник от шины PE щита ЩК …; сдвиг под раскладку плитки стены Г на 71 мм вдоль стены — ось на шве или в центре плитки, привязка по таблице листа; КУП2 — по образцу: Добавлены выводы к вентиляторам: ЭВ4 (ВР1, ванная) и ЭВ5 (ВР3, санузел 2) — группа 3, высота 2389 мм, включение с основным светом, таймер выбега в вентиляторе; и коробки уравнивания потенциалов КУП1 (ванная) и КУП2 (санузел 2) — высота 300 мм, у входа, вне зон 0–2, проводник от шины PE щита ЩК …; сдвиг под раскладку плитки стены А на 27 мм вдоль стены — ось на шве или в центре плитки, привязка по таблице листа; ЩС — щит слаботочный: место и состав; АР1 — точка доступа Wi-Fi: число и места; плинтус пом. 1, 2, 4–14, 16, 17, фартук пом. 1, акцент пом. 5 — артикул изделия не выбран: позиция описана характеристиками («аналог по характеристикам»), артикул выбирается при закупке; пол пом. 3, 15, 20 — пирог пола: стяжка 33 мм и обмазочная гидроизоляция добавлены разработчиком проекта; артикул изделия не выбран: позиция описана характеристиками («аналог по характеристикам»), артикул выбирается при закупке; пол пом. 10 — покрытие пола гаража — предложение исполнителя: выдерживает шины, масло и антигололёдные реагенты, без швов; ИЗ-2, К-11, Кф-1: РО-1 — перенос из-под окна стены А (привязка 1050, 900 мм — был внутри модулей Кх6, Кх1 с мойкой и Кх2 с ПММ, Кф-1) на свободный участок наружной стены Г за окном, у угла со стеной В (у 3500…4100, 100 мм до угла, 110 мм до розетки Р23): прибор открыт, ряд под окном А без коллизии — предложение ОВ (ИЗ-2), на утверждение; окно А без прибора — мощность РО-1 + РО-2 сверить теплотехническим расчётом ОВ (котёл не выбран, К-11); К-11: РО-2, РО-3, РО-4, РО-5, РО-6, РО-7, РО-8, РО-9, РО-10, РО-11 — прибор под окном по оси проёма, ширина ≈ 0,7 ширины окна — предложение ОВ (лист ОВ выводил его сам до, теперь он в данных — один источник для листа, мебели, DXF и IFC); котёл и мощность не выбраны (К-11) — размер по теплотехническому расчёту. См. лист открытых вопросов (лист 8, записи К-1, К-2, К-4, К-7; лист 9, записи К-11, К-13; лист 10, записи ИЗ-2, Кф-1).


Изм.	Кол.уч	Лист	№ док.	Подп.	Дата	ГД-2026-010-АИ			
						Дом 331 м²			
						Общая площадь 270,67* м² · * размеры приняты, не замерены (реестр — л. 8–10, К-1)			
Разраб.		Кырлан А.С.			04.11.26	Дизайн-проект интерьера	Стадия	Лист	Листов
Пров.							РП	126	216
ГИП									
						Реестр марок отделки и позиций альбома (продолжение) М б/м	**Кырлан Александр Сергеевич**		
Н. контр.									
Утв.									

выпуск 04.11.2026 № 2a77323a49 · стр. 130 из 221

Схема расположения развёрток и узлов · 1-й этаж

План этажа «1-й этаж»: марки развёрток по помещениям, выноски узлов, ведомость «марка → лист»

ПРЕДВАРИТЕЛЬНО · не для производства работ · открыто пунктов: 15 (реестр — л. 8–10)

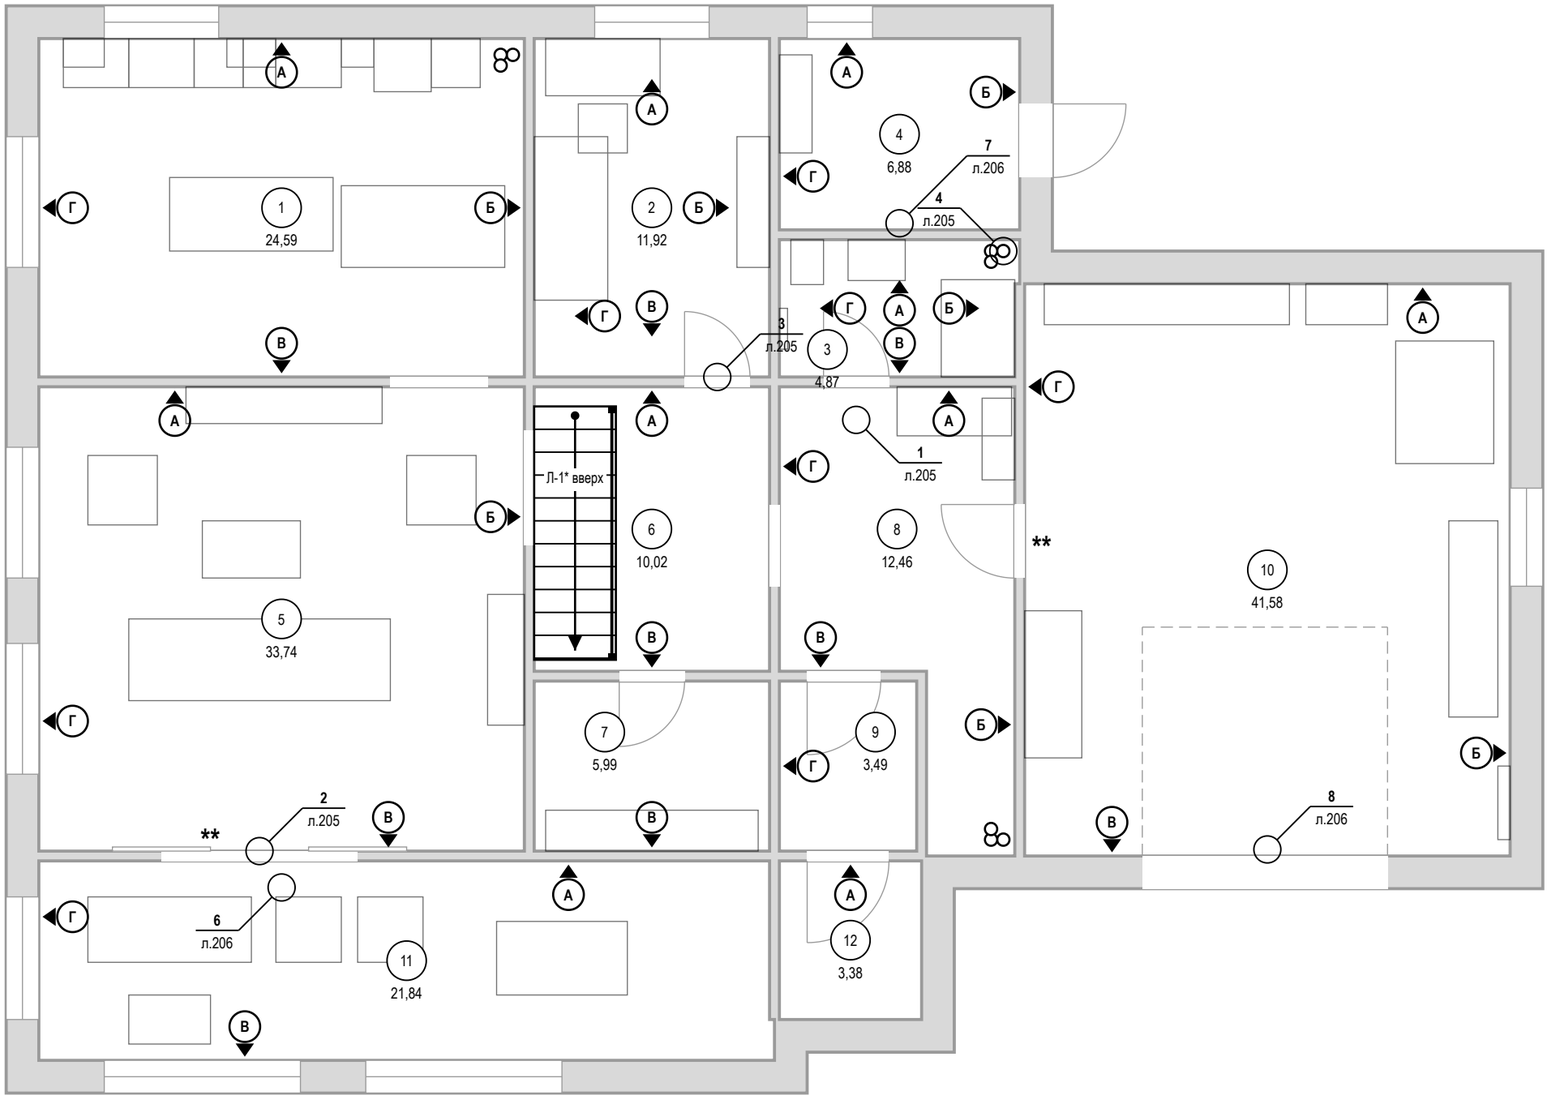

Развёртки и узлы: марка → лист

Марка	Помещение / узел	Лист
А, Б, В, Г	Кухня-столовая (пом. 1)	129–133
А, Б, В, Г	Кабинет-гостевая (пом. 2)	134–139
А, Б, В, Г	Санузел 1 этажа (пом. 3)	140–142
А, Б, Г	Котельная (пом. 4)	143, 144
А, Б, В, Г	Гостиная (пом. 5)	145–149
А, В	Холл с лестницей (пом. 6)	150, 151
В	Кладовая (пом. 7)	152
А, Б, В, Г	Прихожая (пом. 8)	153–156
Г	Тамбур (пом. 9)	157
А, Б, В, Г	Гараж (пом. 10)	158, 159, 161, 162
А, В, Г	Веранда (пом. 11)	164–166
А	Крыльцо (пом. 12)	167
узел 1	Порог 15 мм: мокрая зона — смежное помещение	205
узел 2	Стык покрытий пола с перепадом 30 мм, профиль-переход	205
узел 3	Дверь скрытого монтажа в плоскости стены, плинтус	205
узел 4	Короб стояков К1-1 с люком и звукоизоляцией	205
узел 6	Плинтус МДФ 80×16 мм у окрашенной стены по доске (ламинату)	206
узел 7	Плинтус МДФ 80×16 мм у окрашенной стены по керамограниту (плитке)	206
узел 8	Плинтус ПВХ 100×16 мм у окрашенной стены по наливному полу	206

Допущения и предложения на листе. Основа листа: размеры и контуры этажей подобраны проектировщиком по составу помещений и площадям этажей с картинки 470 px (размеры на ней не читаются); обмер и исходный проект — задание (К-1); высоты: 1-й этаж 2800 мм, мансарда 2700 мм (горизонтальная часть) приняты; скаты кровли мансарды приняты по картинке: колено 1200 мм, уклон 45°, конёк вдоль длинной стороны; проект КР — задание (К-2); наружные стены 400 мм, перегородки 120 мм приняты (К-1); разрешённая мощность 15 кВт принята по типовым ТУ для частного дома (К-4); подрайон климата не задан — принят не северный (жилые от 2,5 м) (К-7). Знак «*» — принято, не замерено (замерить): К-6: Л-1. Знак «**» — предложено, не утверждено (согласовать). См. лист открытых вопросов (лист 8, записи К-1, К-2, К-4, К-6, К-7; лист 9, запись К-9).

Условные обозначения

- А — марка развёртки: буква стены, стрелка — взгляд
- выноска узла: над полкой — узел, под полкой — лист
- 1 — номер помещения, площадь м²

1000 мм · печать 1:1

Примечания

1. Развёртки — вид на стену изнутри помещения; буквы стен — одна система на весь альбом (как на листах выводов, плитки и отделки).
2. Стены без электроточек, мебели, декора и акцентной отделки развёрток не имеют: их отделка — по ведомости отделки помещений.
3. Узлы — на листе узлов; места применения — по выноскам этого листа и ведомости «марка → лист».

Изм.	Кол.уч	Лист	№ док.	Подп.	Дата
Разраб.		Кырлан А.С.			04.11.26
Пров.					
ГИП					
Н. контр.					
Утв.					

ГД-2026-010-АИ

Дом 331 м²

Общая площадь 270,67* м² · * размеры приняты, не замерены (реестр — л. 8–10, К-1)

Дизайн-проект интерьера

Стадия	Лист	Листов
РП	127	216

Схема расположения развёрток и узлов · 1-й этаж

М 1:75


Кырлан Александр Сергеевич

выпуск 04.11.2026 № 2a77323a49 · стр. 131 из 221

Схема расположения развёрток и узлов · Мансарда

План этажа «Мансарда»: марки развёрток по помещениям, выноски узлов, ведомость «марка → лист»

ПРЕДВАРИТЕЛЬНО · не для производства работ · открыто пунктов: 15 (реестр — л. 8–10)

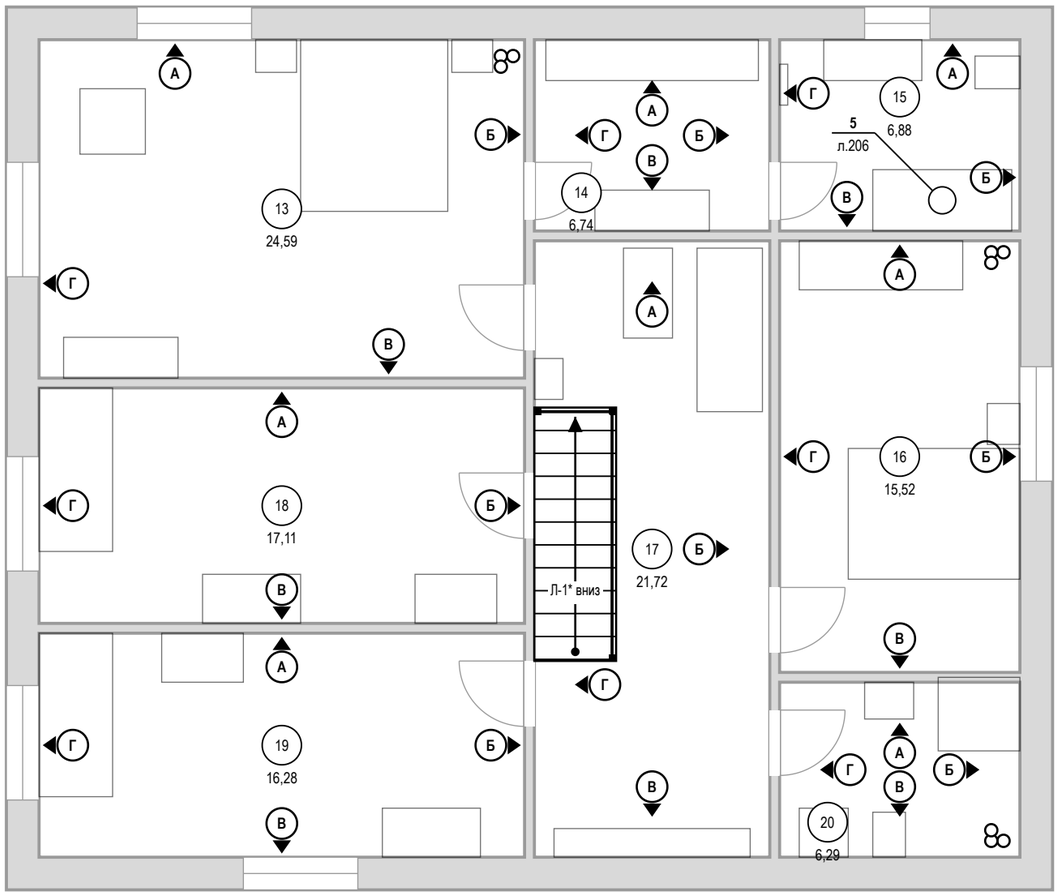

Допущения и предложения на листе

Основа листа: размеры и контуры этажей подобраны проектировщиком по составу помещений и площадям этажей с картинки 470 px (размеры на ней не читаются); обмер и исходный проект — задание (К-1); высоты: 1-й этаж 2800 мм, мансарда 2700 мм (горизонтальная часть) приняты; скаты кровли мансарды приняты по картинке: колено 1200 мм, уклон 45°, конёк вдоль длинной стороны; проект КР — задание (К-2); наружные стены 400 мм, перегородки 120 мм приняты (К-1); разрешённая мощность 15 кВт принята по типовым ТУ для частного дома (К-4); подрайон климата не задан — принят не северный (жилые от 2,5 м) (К-7).

Знак «*» — принято, не замерено и не подтверждено (замерить на объекте): К-2: отметка чистого пола этажа «Мансарда» +3,150 — принята без источника, все отметки мансарды считаются от неё; К-6: Л-1 — габарит марша снят с картинки заказчика (11 проступей в холле 3,6 м), а до отм. +3,150 нужно 18 подъёмов — одномаршевая не встаёт: решение по К-6.

См. лист открытых вопросов (лист 8, записи К-1, К-2, К-4, К-6, К-7).

Условные обозначения

- А — марка развёртки: буква стены, стрелка — взгляд
- выноска узла: над полкой — узел, под полкой — лист
- 1 — номер помещения, площадь м²

1000 мм · печать 1:1

Примечания

1. Развёртки — вид на стену изнутри помещения; буквы стен — одна система на весь альбом (как на листах выводов, плитки и отделки).
2. Стены без электроточек, мебели, декора и акцентной отделки развёрток не имеют: их отделка — по ведомости отделки помещений.
3. Узлы — на листе узлов; места применения — по выноскам этого листа и ведомости «марка → лист».

Развёртки и узлы: марка → лист

Марка	Помещение / узел	Лист
А	Спальня мастер (пом. 13)	168, 169
Б	Спальня мастер (пом. 13)	170
В	Спальня мастер (пом. 13)	171
Г	Спальня мастер (пом. 13)	172
А, Б	Гардеробная мастер (пом. 14)	173
В, Г	Гардеробная мастер (пом. 14)	174
А, Б	Санузел мастер (пом. 15)	175, 177
В, Г	Санузел мастер (пом. 15)	176, 177
А	Спальня 2 (пом. 16)	178, 179
Б	Спальня 2 (пом. 16)	180
В	Спальня 2 (пом. 16)	181, 182
Г	Спальня 2 (пом. 16)	183
А	Холл мансарды (пом. 17)	184
Б	Холл мансарды (пом. 17)	185
В	Холл мансарды (пом. 17)	187
Г	Холл мансарды (пом. 17)	188
А	Спальня 3 (пом. 18)	190
Б	Спальня 3 (пом. 18)	191
В	Спальня 3 (пом. 18)	192, 193
Г	Спальня 3 (пом. 18)	194
А	Спальня 4 (пом. 19)	195
Б	Спальня 4 (пом. 19)	196
В	Спальня 4 (пом. 19)	197, 198
Г	Спальня 4 (пом. 19)	199
А, Б	Санузел 2 (пом. 20)	200, 201, 202
В, Г	Санузел 2 (пом. 20)	203, 204
узел 5	Гидроизоляция санузла: заход на стены 200 мм, примыкание ванны	206

Изм.	Кол.уч	Лист	№ док.	Подп.	Дата
Разраб.		Кырлан А.С.			04.11.26
Пров.					
ГИП					
Н. контр.					
Утв.					

ГД-2026-010-АИ

Дом 331 м²

Общая площадь 270,67* м² · * размеры приняты, не замерены (реестр — л. 8–10, К-1)

Дизайн-проект интерьера

Стадия	Лист	Листов
РП	128	216

Схема расположения развёрток и узлов · Мансарда

М 1:75

Кырлан Александр Сергеевич


выпуск 04.11.2026 № 2a77323a49 · стр. 132 из 221

Развёртка стены А. Кухня-столовая (пом. 1), кухонный фронт

Кухня-столовая (пом. 1) · вид изнутри помещения · размеры в мм, отметки в м от ±0,000 (чистый пол 1-го этажа)


ПРЕДВАРИТЕЛЬНО · не для производства работ · открыто пунктов: 15 (реестр — л. 8–10)

Развёртка стены А

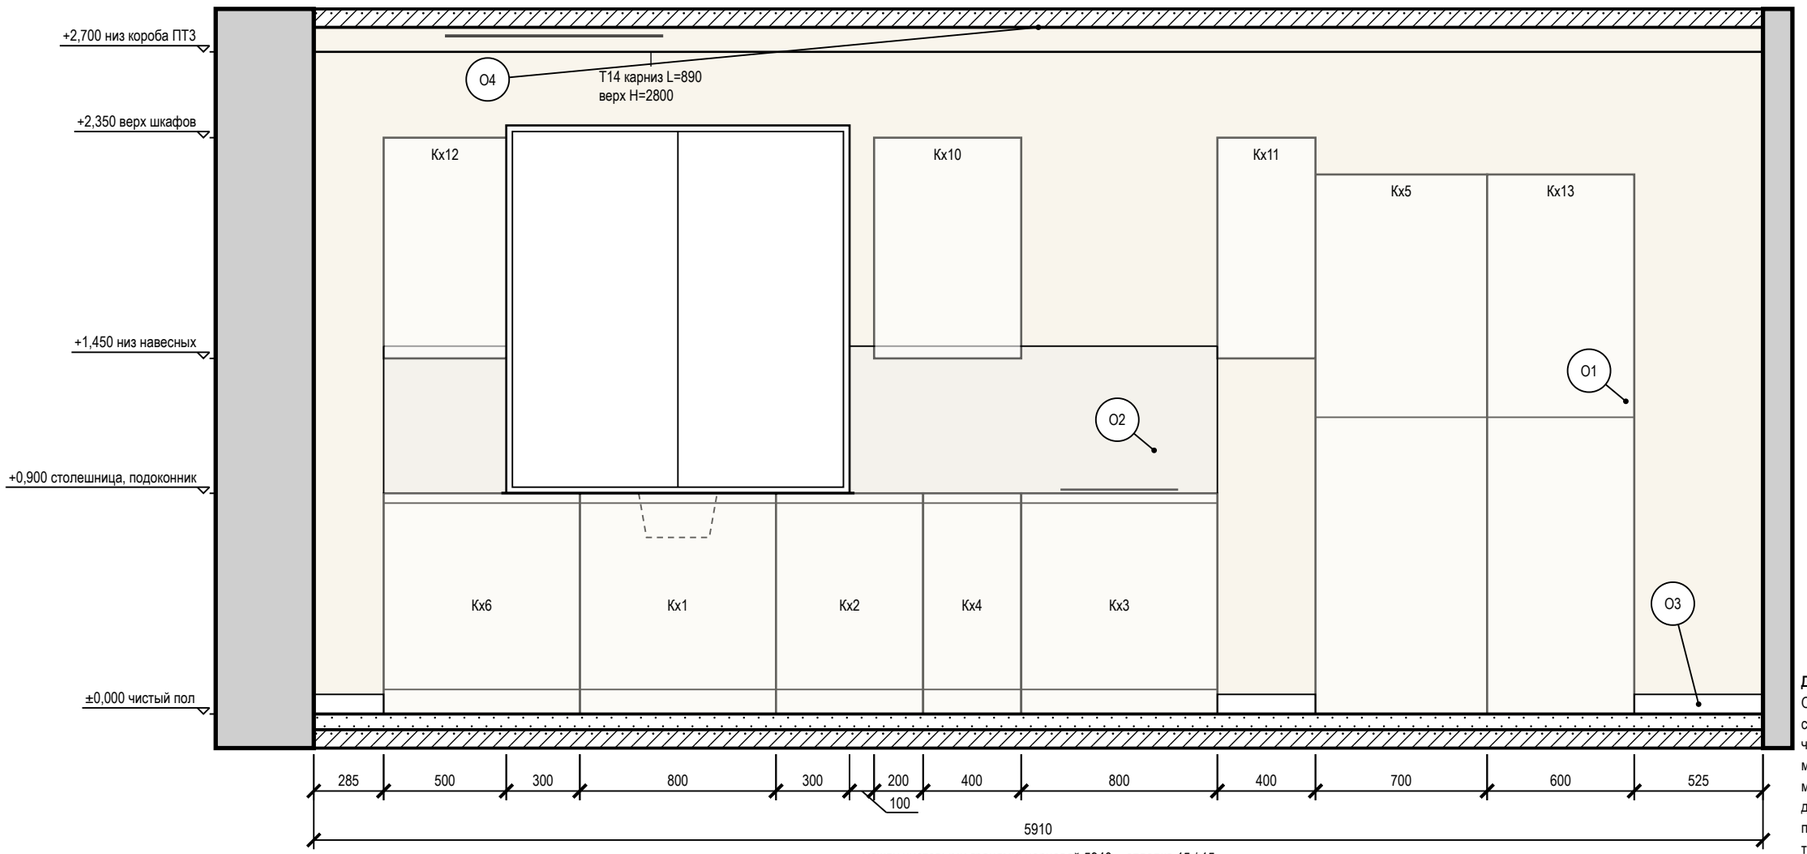

между чистовыми гранями: черновой 5940 − отделка 15 / 15

Схема развёрток (М 1:100)

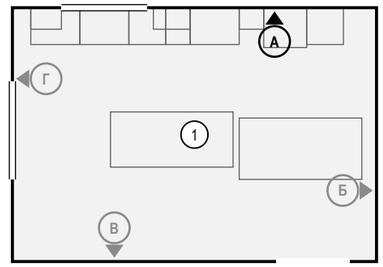

Допущения и предложения на листе

Основа листа: размеры и контуры этажей подобраны проектировщиком по составу помещений и площадям этажей с картинки 470 px (размеры на ней не читаются); обмер и исходный проект — задание (К-1); высоты: 1-й этаж 2800 мм, мансарда 2700 мм (горизонтальная часть) приняты; скаты кровли мансарды приняты по картинке: колено 1200 мм, уклон 45°, конёк вдоль длинной стороны; проект КР — задание (К-2); наружные стены 400 мм, перегородки 120 мм приняты (К-1); разрешённая мощность 15 кВт принята по типовым ТУ для частного дома (К-4); подрайон климата не задан — принят не северный (жилые от 2,5 м) (К-7).

См. лист открытых вопросов (лист 8, записи К-1, К-2, К-4, К-7).

Условные обозначения

- мебель и приборы — фасад по расстановке (условно)
- карниз (шина) и шторы в собранном виде: марка Т, длина L, верх H
- окно: проём, рама, подоконник
- стены и перекрытия в сечении
- плитка: сетка швов по формату, ▲ — ось старта
- окраска: тон — цвет по коду производителя (условно)
- О1 — марка отделки по реестру отделки альбома
- А — марка развёртки: буква стены, стрелка — взгляд

Ведомость отделки (на листе)

Марка	Поверхность	Материал, изделие	Цвет, код	Кол.
О1	стены	окраска, Tikkurila Luja 7, шелковисто-матовая, подготовка К3	NCS S 0804-Y30R «S 0804-Y30R»	12,4 м²
О2	фартук	керамогранит, аналог: керамогранит матовый, тон F497, затирка CG2WA	#F1F1EC «тон Paper F497»	1,2 м²
О3	плинтус	плинтус МДФ, h 80 мм, аналог: плинтус МДФ под окраску 80×16 мм, полуглянцевая	NCS S 0804-Y30R «S 0804-Y30R»	1,2 м
О4	потолок	окраска, Tikkurila Luja 7, матовая, подготовка Q3	NCS S 0804-Y30R «S 0804-Y30R»	24,6 м²

Примечания

1. Развёртки — вид на стену изнутри помещения, по часовой стрелке; расположение — на схеме листа и на листе 127; размеры — в мм по чистовым поверхностям; отметки — в м от ±0,000 (чистый пол 1-го этажа); высоты Н — от чистого пола помещения до оси изделия, у декора — до центра.
2. Стена А показана двумя видами: здесь — архитектурная развёртка (мебель, отделка, проёмы, высоты), электроточки и выводы ВК с привязками и таблицей — на листе 130 («Привязки»).
3. Схема мебели, приборов и декора не является технической документацией для производства мебели; габариты — по паспортам изделий.
4. Карнизы (шины) — по ведомости текстиля декоратора: длина L и верх Н на развёртке — те же числа, что в ведомости; крепление — до окраски потолка.
5. Потолок — у каждой стены свой, по плану потолков (НШ1, ПТ3); ступени — зоной, кромка короба перед нишей — тонкой линией; в поле потолка: ПТ1 +2,550, ПТ2 +2,600.

1000 мм · печать 1:1

Изм.	Кол.уч	Лист	№ док.	Подп.	Дата
Разраб.		Кырлан А.С.			04.11.26
Пров.					
ГИП					
Н. контр.					
Утв.					

ГД-2026-010-АИ

Дом 331 м²

Общая площадь 270,67* м² · * размеры приняты, не замерены (реестр — л. 8–10, К-1)

Дизайн-проект интерьера

Стадия	Лист	Листов
РП	129	216

Развёртка стены А. Кухня-столовая (пом. 1), кухонный фронт

М 1:25

Кырлан Александр Сергеевич

выпуск 04.11.2026 № 2a77323a49 · стр. 133 из 221

Привязки электроточек и выводов ВК, стена А. Кухня-столовая (пом. 1)

Кухня-столовая (пом. 1) · вид изнутри помещения · привязки в мм, отметки в м · к развёртке на листе 129

ПРЕДВАРИТЕЛЬНО · не для производства работ · открыто пунктов: 15 (реестр — л. 8–10)

Развёртка стены А: электроточки и выводы


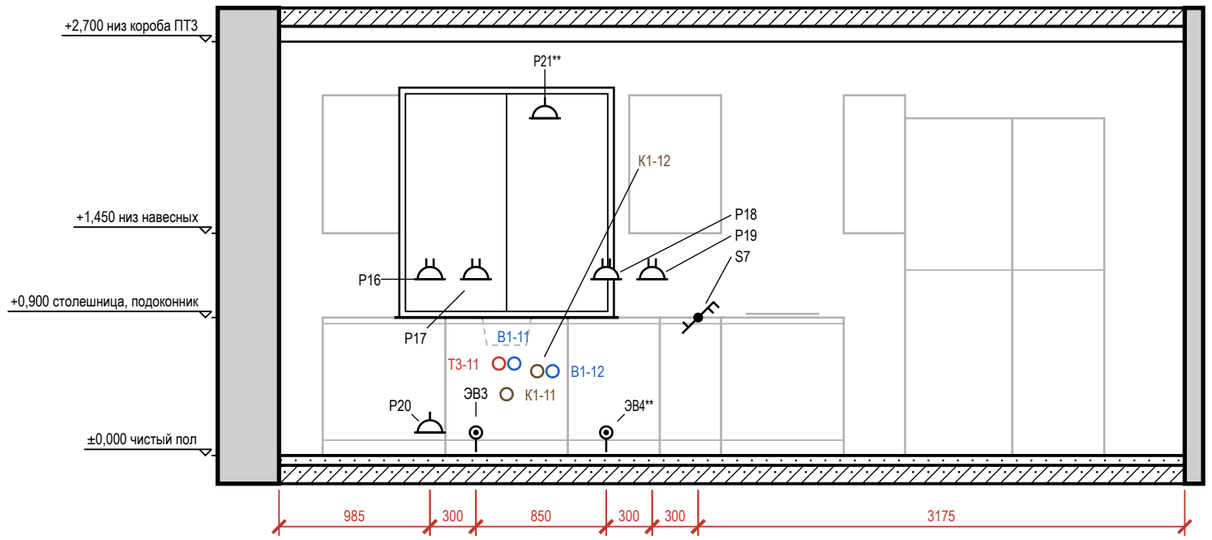


Таблица привязок электроточек и выводов

Марка	Назначение	От угла, мм	Н от пола, мм	Примечание
P20	розетка: холодильник встроенный Кх5 (розетка в соседнем модуле)	985	150	гр. 10
P16	розетка: фартук: мелкая техника	985	1150	рамка 2 поста, гр. 9
ЭВ3	вывод кабеля: варочная панель Кх3	1285	150	гр. 11
P17	розетка: фартук: мелкая техника	1285	1150	рамка 2 поста, гр. 9
T3-11	горячая вода — мойка кухонная	1435	600*	межос. 100
K1-11	канализация — мойка кухонная	1485	400*	Ø50
B1-11	холодная вода — мойка кухонная	1535	600*	межос. 100
K1-12	канализация — посудомоечная машина	1685	550*	Ø40; слив ПММ в шкафу мойки
P21**	розетка: вытяжка над варочной панелью Кх3 (розетка за съёмной панелью)	1735	2200	гр. 10
B1-12	холодная вода — посудомоечная машина	1785	550*	кран ПММ в шкафу мойки
ЭВ4**	вывод кабеля: духовой шкаф Кх3 (вывод в соседнем модуле)	2135	150	гр. 15
P18	розетка: фартук: мелкая техника	2135	1150	рамка 2 поста, гр. 9
P19	розетка: фартук: мелкая техника	2435	1150	рамка 2 поста, гр. 9
S7	выключатель	2735	900	гр. 1

Схема развёрток (М 1:100)

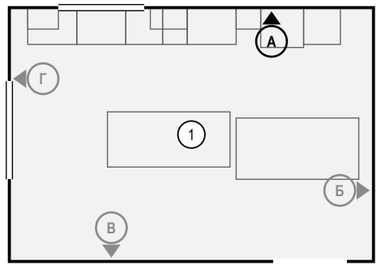

Условные обозначения

- розетка с заземляющим контактом; у знака — марка, ×N постов в рамке, гр. — группа щита, Н — высота оси, мм
- вывод кабеля для подключения прибора (без розетки), марка ЭВ
- выключатель одноклавишный
- выключатель двухклавишный (флажков — по числу клавиш)
- выключатель с проходной или перекрёстной клавишей (обратный флажок); тип клавиши — в подписи
- вывод В1 (код — в ведомости привязок)
- вывод Т3 (код — в ведомости привязок)
- вывод К1 (код — в ведомости привязок)
- привязки точек и выводов от угла и от пола, мм
- А — марка развёртки: буква стены, стрелка — взгляд

Примечания

1. Вид «Привязки» стены А — электроточки и выводы ВК; архитектурная развёртка (мебель, отделка, проёмы, высоты) — на листе 129, расположение — на листе 127. Мебель и приборы — подложкой для ориентира; их марки и обозначения мебели, проёмов и стен — там же.
2. Привязки — в мм: по горизонтали от левого чистового угла стены до оси изделия, Н — от чистого пола до оси; все точки — в таблице привязок. Красная цепочка — привязки по осям; точки ближе 240 мм одна к другой в цепочку не дробятся — их привязки только в таблице.
3. У знака — марка электроточки (Р — розетка, S — выключатель, Св — светильник, ЭВ — вывод кабеля); посты в рамке и группа щита — в графе «Примечание»; группы по клавишам выключателя — на листе выключателей.
4. Коды выводов ВК: В1 — холодная вода, Т3 — горячая вода, К1 — канализация; номер после дефиса — номер вывода на листе выводов сантехники; * — высота принята по типовой практике монтажа, окончательно — по паспорту прибора.
5. Выводы кухонной техники — по утверждённому проекту кухни: привязки выводов даются от осей модулей гарнитура.

Допущения и предложения на листе

Основа листа: размеры и контуры этажей подобраны проектировщиком по составу помещений и площадям этажей с картинки 470 px (размеры на ней не читаются); обмер и исходный проект — задание (К-1); высоты: 1-й этаж 2800 мм, мансарда 2700 мм (горизонтальная часть) приняты; скаты кровли мансарды приняты по картинке: колено 1200 мм, уклон 45°, конёк вдоль длинной стороны; проект КР — задание (К-2); наружные стены 400 мм, перегородки 120 мм приняты (К-1); разрешённая мощность 15 кВт принята по типовым ТУ для частного дома (К-4); подрайон климата не задан — принят не северный (жилые от 2,5 м) (К-7).

Знак «**» — предложение проектировщика, заказчиком не утверждено (согласовать с заказчиком): Р21 — высота 2200 мм выше нормы 1 м (ПУЭ 6.6.30) по назначению: питание вытяжки над варочной панелью Кх3, розетка за съёмной панелью; ЭВ4 — по образцу: Добавлены выводы к вентиляторам: ЭВ4 (ВР1, ванная) и ЭВ5 (ВР3, санузел 2) — группа 3, высота 2389 мм, включение с основным светом, таймер выбега в вентиляторе; и коробки уравнивания потенциалов КУП1 (ванная) и КУП2 (санузел 2) — высота 300 мм, у входа, вне зон 0–2, проводник от шины РЕ щита ЩК …; сдвиг под раскладку плитки стены Б на 100 мм вдоль стены и на 14 мм выше — ось на шве или в центре плитки, привязка по таблице листа.

См. лист открытых вопросов (лист 8, записи К-1, К-2, К-4, К-7).

1000 мм · печать 1:1

Изм.	Кол.уч	Лист	№ док.	Подп.	Дата
Разраб.		Кырлан А.С.			04.11.26
Пров.					
ГИП					
Н. контр.					
Утв.					

ГД-2026-010-АИ

Дом 331 м²

Общая площадь 270,67* м² · * размеры приняты, не замерены (реестр — л. 8–10, К-1)

Дизайн-проект интерьера

Стадия	Лист	Листов
РП	130	216

Привязки электроточек и выводов ВК, стена А. Кухня-столовая (пом. 1)

М 1:40

Кырлан Александр Сергеевич

выпуск 04.11.2026 № 2a77323a49 · стр. 134 из 221

Развёртка стены Б. Кухня-столовая (пом. 1)

Кухня-столовая (пом. 1) · вид изнутри помещения · размеры в мм, отметки в м от ±0,000 (чистый пол 1-го этажа)

ПРЕДВАРИТЕЛЬНО · не для производства работ · открыто пунктов: 15 (реестр — л. 8–10)

Развёртка стены Б


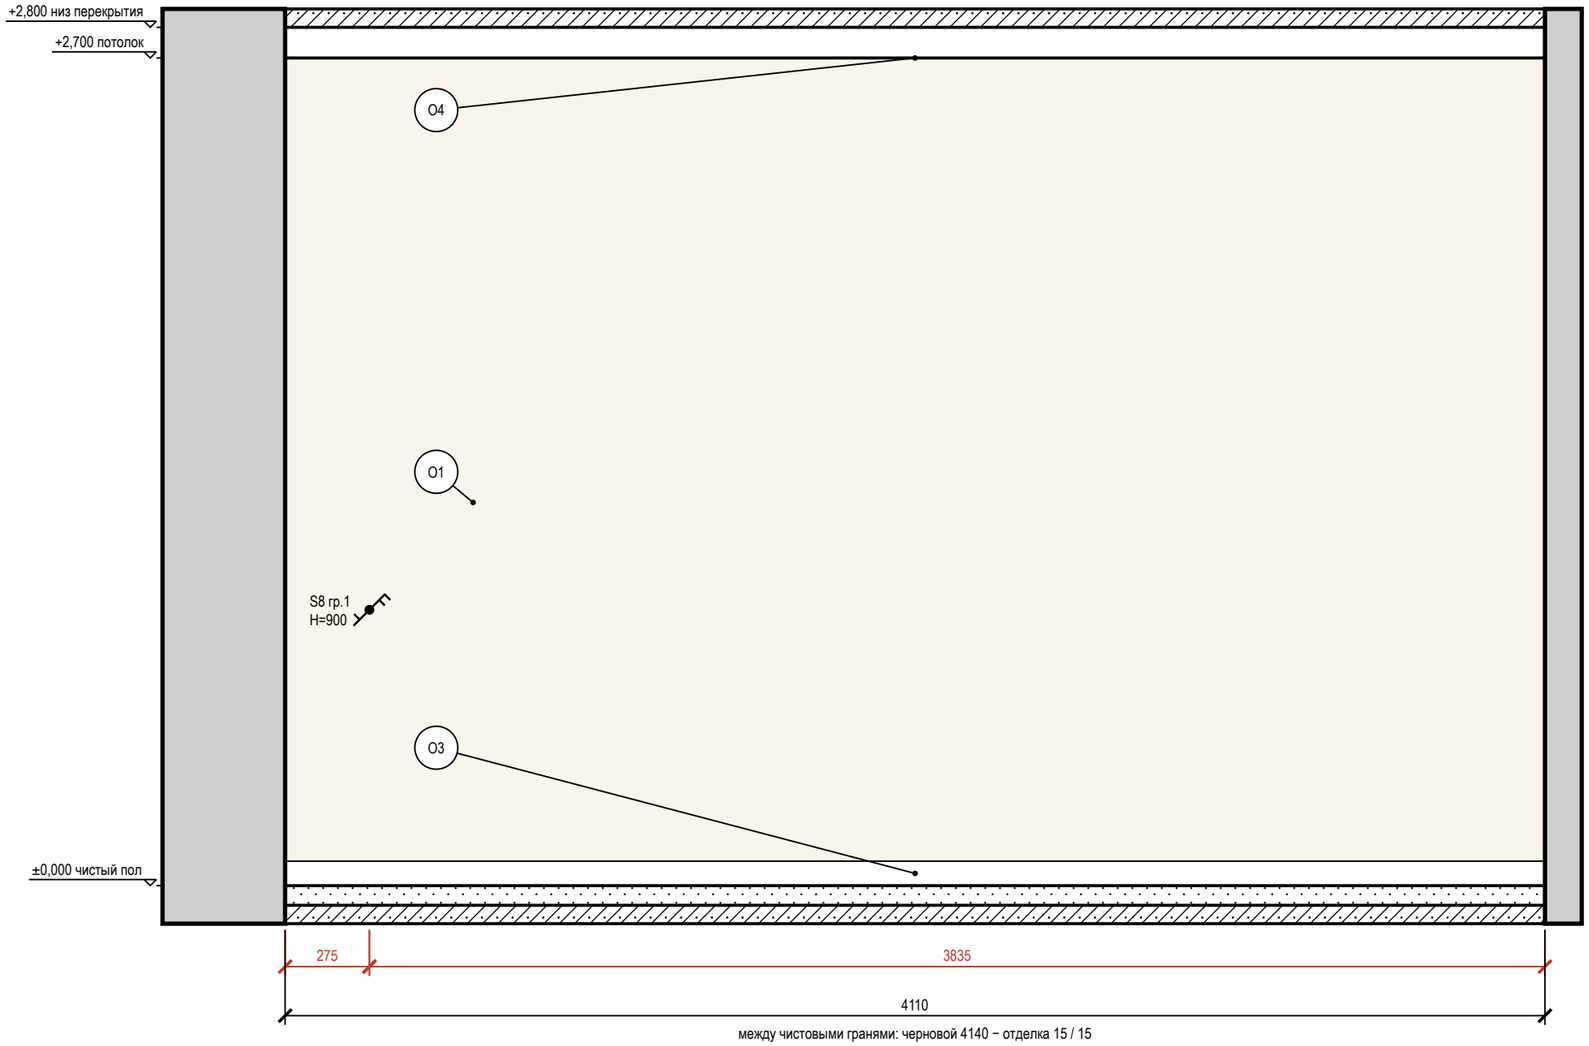


Схема развёрток (М 1:100)

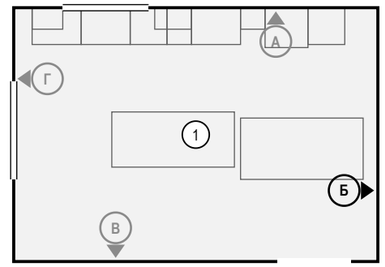

Условные обозначения

- выключатель одноклавишный
- выключатель двухклавишный (флажков — по числу клавиш)
- выключатель с проходной или перекрёстной клавишей (обратный флажок); тип клавиши — в подписи
- привязки точек и выводов от угла и от пола, мм
- мебель и приборы — фасад по расстановке (условно)
- стены и перекрытия в сечении
- окраска: тон — цвет по коду производителя (условно)
- О1 — марка отделки по реестру отделки альбома
- А — марка развёртки: буква стены, стрелка — взгляд

Ведомость отделки (на листе)

Марка	Поверхность	Материал, изделие	Цвет, код	Кол.
О1	стены	окраска, Tikkurila Luja 7, шелковисто-матовая, подготовка К3	NCS S 0804-Y30R «S 0804-Y30R»	11,1 м²
О3	плинтус	плинтус МДФ, h 80 мм, аналог: плинтус МДФ под окраску 80×16 мм, полуглянцевая	NCS S 0804-Y30R «S 0804-Y30R»	4,1 м
О4	потолок	окраска, Tikkurila Luja 7, матовая, подготовка Q3	NCS S 0804-Y30R «S 0804-Y30R»	24,6 м²

Допущения и предложения на листе

Основа листа: размеры и контуры этажей подобраны проектировщиком по составу помещений и площадям этажей с картинки 470 px (размеры на ней не читаются); обмер и исходный проект — задание (К-1); высоты: 1-й этаж 2800 мм, мансарда 2700 мм (горизонтальная часть) приняты; скаты кровли мансарды приняты по картинке: колено 1200 мм, уклон 45°, конёк вдоль длинной стороны; проект КР — задание (К-2); наружные стены 400 мм, перегородки 120 мм приняты (К-1); разрешённая мощность 15 кВт принята по типовым ТУ для частного дома (К-4); подрайон климата не задан — принят не северный (жилые от 2,5 м) (К-7).

См. лист открытых вопросов (лист 8, записи К-1, К-2, К-4, К-7).

Примечания

1. Развёртки — вид на стену изнутри помещения, по часовой стрелке; расположение — на схеме листа и на листе 127; размеры — в мм по чистовым поверхностям; отметки — в м от ±0,000 (чистый пол 1-го этажа); высоты Н — от чистого пола помещения до оси изделия, у декора — до центра.
2. Красная цепочка — привязки электроточек и выводов по осям от угла чистовых стен; высота Н — у знака, от чистого пола до оси; высоты мебели, проёмов и границ отделки — колонкой отметок слева. Стена с 5 и более точками или с мелкими звеньями привязок показана двумя видами: архитектурная развёртка (мебель, отделка, проёмы, высоты) и вид «Привязки» на отдельном листе — точки и выводы с марками, одна цепочка по осям и таблица привязок (каждая точка — строка).
3. У знака электроточки: марка (Р — розетка, S — выключатель, Св — светильник, ЭВ — вывод кабеля), ×N — число постов в рамке, гр. — группа щита, Н — высота оси от чистого пола, мм; группы по клавишам выключателя — на листе выключателей.
4. Схема мебели, приборов и декора не является технической документацией для производства мебели; габариты — по паспортам изделий.
5. Потолок — у каждой стены свой, по плану потолков (ПТ3); ступени — зоной, кромка короба перед нишей — тонкой линией; в поле потолка: ПТ1 +2,550, ПТ2 +2,600.

1000 мм · печать 1:1

Изм.	Кол.уч	Лист	№ док.	Подп.	Дата
Разраб.		Кырлан А.С.			04.11.26
Пров.					
ГИП					
Н. контр.					
Утв.					

ГД-2026-010-АИ

Дом 331 м²

Общая площадь 270,67* м² · * размеры приняты, не замерены (реестр — л. 8–10, К-1)

Дизайн-проект интерьера

Стадия	Лист	Листов
РП	131	216

Развёртка стены Б. Кухня-столовая (пом. 1)

М 1:20

Кырлан Александр Сергеевич


выпуск 04.11.2026 № 2a77323a49 · стр. 135 из 221

Развёртка стены В. Кухня-столовая (пом. 1)

Кухня-столовая (пом. 1) · вид изнутри помещения · размеры в мм, отметки в м от ±0,000 (чистый пол 1-го этажа)


ПРЕДВАРИТЕЛЬНО · не для производства работ · открыто пунктов: 15 (реестр — л. 8–10)

Развёртка стены В

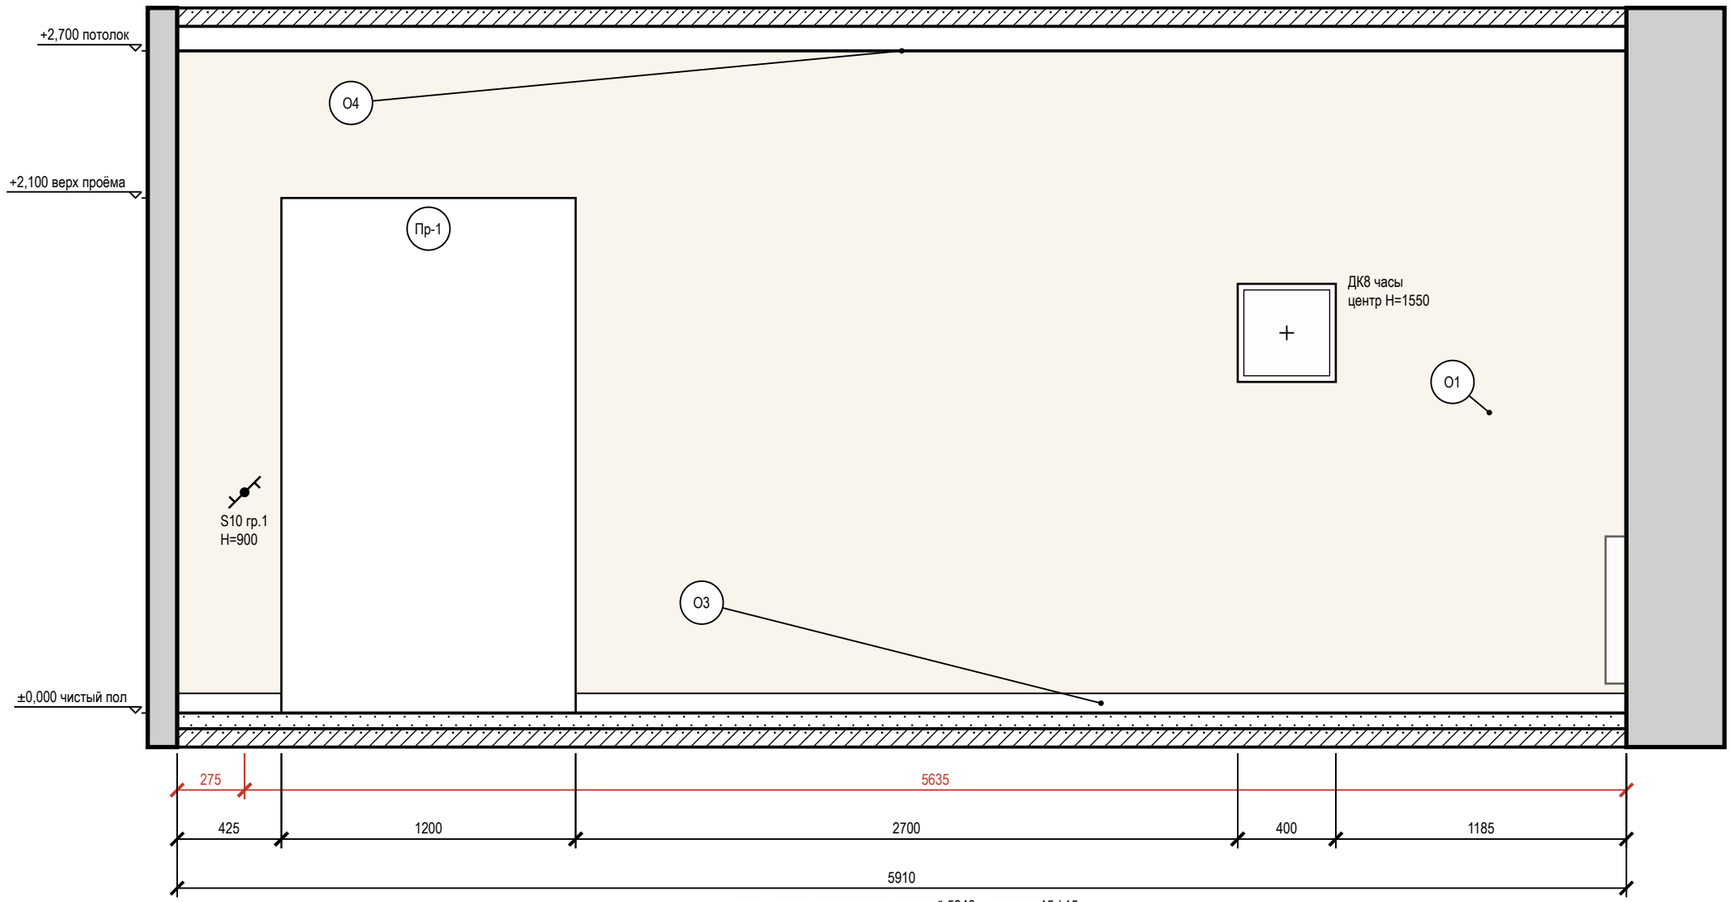

между чистовыми гранями: черновой 5940 − отделка 15 / 15

Схема развёрток (М 1:100)

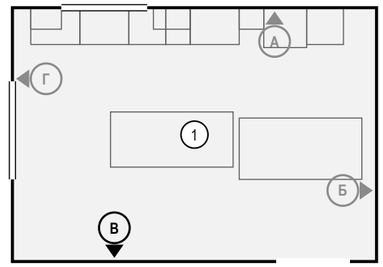

Условные обозначения

- выключатель одноклавишный
- выключатель с проходной или перекрёстной клавишей (обратный флажок); тип клавиши — в подписи
- привязки точек и выводов от угла и от пола, мм
- мебель и приборы — фасад по расстановке (условно)
- картина (декор): марка Д, крест — центр, Н — высота центра, мм
- дверной проём; марка двери — в кружке
- радиатор отопления; марка — по плану отопления
- стены и перекрытия в сечении
- окраска: тон — цвет по коду производителя (условно)
- О1 — марка отделки по реестру отделки альбома
- А — марка развёртки: буква стены, стрелка — взгляд

Ведомость отделки (на листе)

Марка	Поверхность	Материал, изделие	Цвет, код	Кол.
О1	стены	окраска, Tikkurila Luja 7, шелковисто-матовая, подготовка К3	NCS S 0804-Y30R «S 0804-Y30R»	13,4 м²
О3	плинтус	плинтус МДФ, h 80 мм, аналог: плинтус МДФ под окраску 80×16 мм, полуглянцевая	NCS S 0804-Y30R «S 0804-Y30R»	4,7 м
О4	потолок	окраска, Tikkurila Luja 7, матовая, подготовка Q3	NCS S 0804-Y30R «S 0804-Y30R»	24,6 м²

Допущения и предложения на листе

Основа листа: размеры и контуры этажей подобраны проектировщиком по составу помещений и площадям этажей с картинки 470 px (размеры на ней не читаются); обмер и исходный проект — задание (К-1); высоты: 1-й этаж 2800 мм, мансарда 2700 мм (горизонтальная часть) приняты; скаты кровли мансарды приняты по картинке: колено 1200 мм, уклон 45°, конёк вдоль длинной стороны; проект КР — задание (К-2); наружные стены 400 мм, перегородки 120 мм приняты (К-1); разрешённая мощность 15 кВт принята по типовым ТУ для частного дома (К-4); подрайон климата не задан — принят не северный (жилые от 2,5 м) (К-7).

См. лист открытых вопросов (лист 8, записи К-1, К-2, К-4, К-7).

Примечания

1. Развёртки — вид на стену изнутри помещения, по часовой стрелке; расположение — на схеме листа и на листе 127; размеры — в мм по чистовым поверхностям; отметки — в м от ±0,000 (чистый пол 1-го этажа); высоты Н — от чистого пола помещения до оси изделия, у декора — до центра.
2. Красная цепочка — привязки электроточек и выводов по осям от угла чистовых стен; высота Н — у знака, от чистого пола до оси; высоты мебели, проёмов и границ отделки — колонкой отметок слева. Стена с 5 и более точками или с мелкими звеньями привязок показана двумя видами: архитектурная развёртка (мебель, отделка, проёмы, высоты) и вид «Привязки» на отдельном листе — точки и выводы с марками, одна цепочка по осям и таблица привязок (каждая точка — строка).
3. У знака электроточки: марка (Р — розетка, S — выключатель, Св — светильник, ЭВ — вывод кабеля), ×N — число постов в рамке, гр. — группа щита, Н — высота оси от чистого пола, мм; группы по клавишам выключателя — на листе выключателей.
4. Схема мебели, приборов и декора не является технической документацией для производства мебели; габариты — по паспортам изделий.
5. Картины и зеркала крепить к основанию по паспорту изделия (закладные и анкеры — в перечне скрытых работ); крест — ось центра предмета.
6. Потолок — у каждой стены свой, по плану потолков (ПТ3); ступени — зоной, кромка короба перед нишей — тонкой линией; в поле потолка: ПТ1 +2,550, ПТ2 +2,600.

1000 мм · печать 1:1

Изм.	Кол.уч	Лист	№ док.	Подп.	Дата
Разраб.		Кырлан А.С.			04.11.26
Пров.					
ГИП					
Н. контр.					
Утв.					

ГД-2026-010-АИ

Дом 331 м²

Общая площадь 270,67* м² · * размеры приняты, не замерены (реестр — л. 8–10, К-1)

Дизайн-проект интерьера	Стадия	Лист	Листов
	РП	132	216

Развёртка стены В. Кухня-столовая (пом. 1)

М 1:25

Кырлан Александр Сергеевич

выпуск 04.11.2026 № 2a77323a49 · стр. 136 из 221

Развёртка стены Г. Кухня-столовая (пом. 1)

Кухня-столовая (пом. 1) · вид изнутри помещения · размеры в мм, отметки в м от ±0,000 (чистый пол 1-го этажа)

Развёртка стены Г


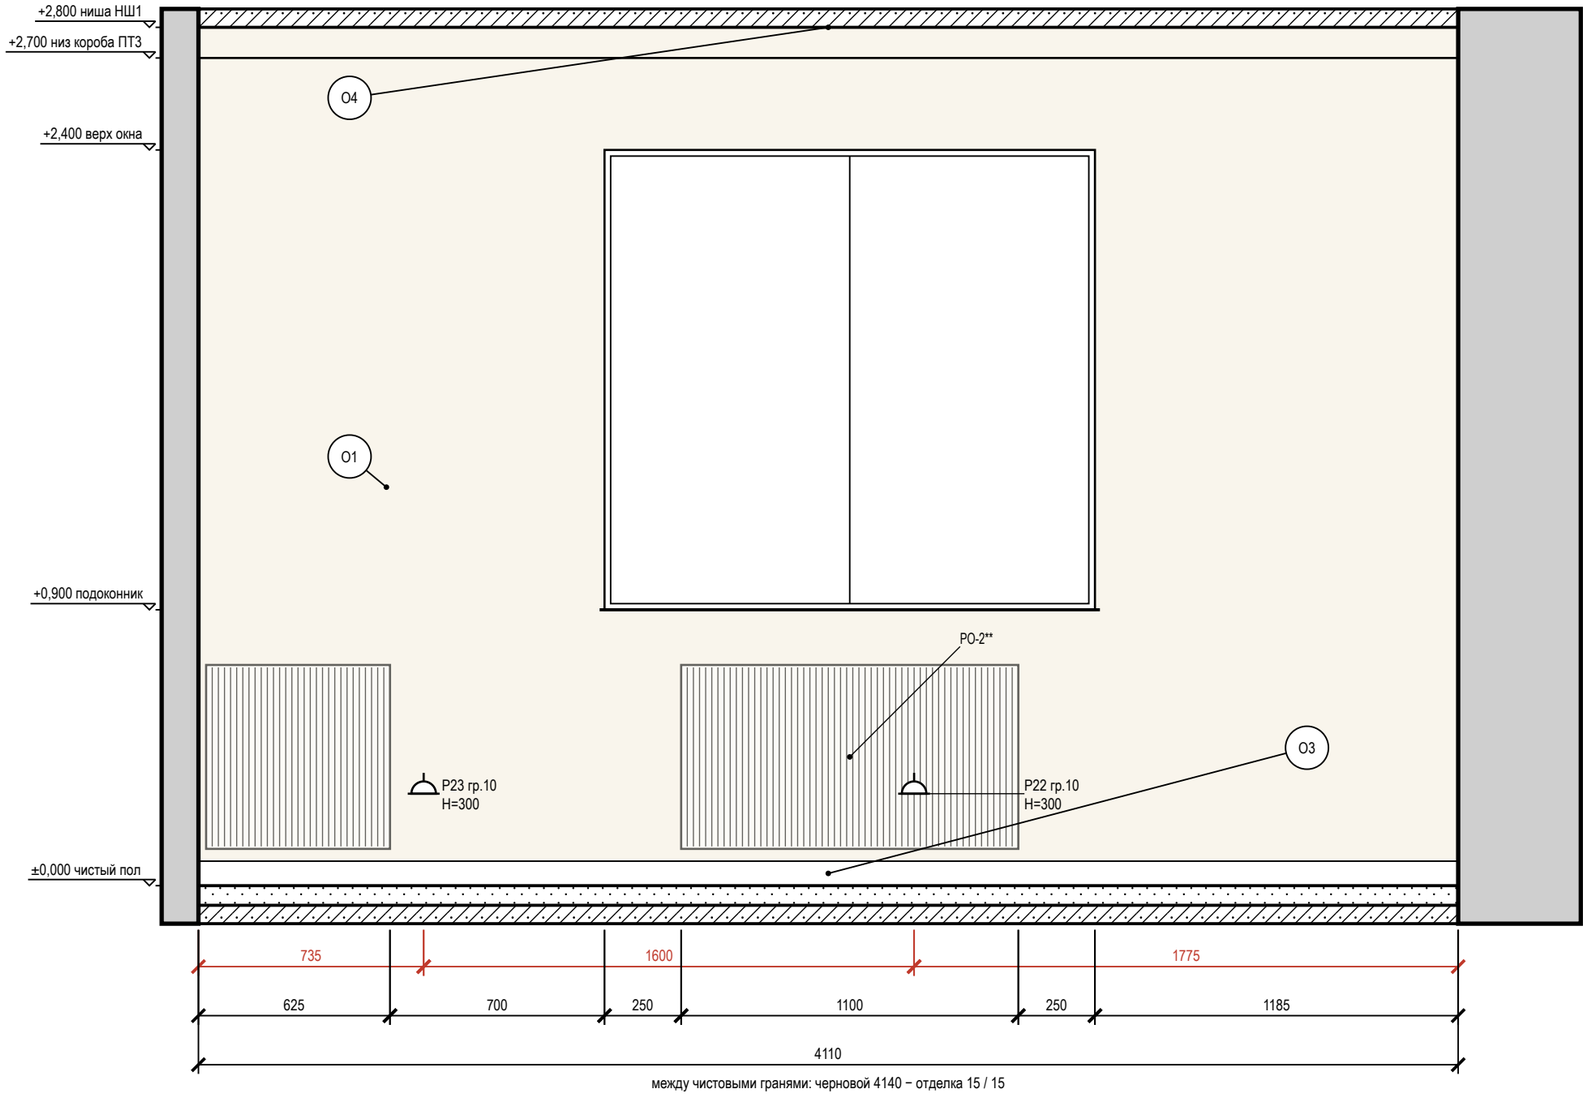


Схема развёрток (М 1:100)

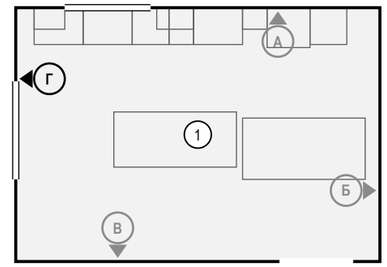

Условные обозначения

- розетка с заземляющим контактом; у знака — марка, ×N постов в рамке, гр. — группа щита, H — высота оси, мм
- привязки точек и выводов от угла и от пола, мм
- мебель и приборы — фасад по расстановке (условно)
- окно: проём, рама, подоконник
- радиатор отопления; марка — по плану отопления
- стены и перекрытия в сечении
- окраска: тон — цвет по коду производителя (условно)
- О1 — марка отделки по реестру отделки альбома
- А — марка развёртки: буква стены, стрелка — взгляд

Ведомость отделки (на листе)

Марка	Поверхность	Материал, изделие	Цвет, код	Кол.
О1	стены	окраска, Tikkurila Luja 7, шелковисто-матовая, подготовка К3	NCS S 0804-Y30R «S 0804-Y30R»	9,1 м²
О3	плинтус	плинтус МДФ, h 80 мм, аналог: плинтус МДФ под окраску 80×16 мм, полуглянцевая	NCS S 0804-Y30R «S 0804-Y30R»	4,1 м
О4	потолок	окраска, Tikkurila Luja 7, матовая, подготовка Q3	NCS S 0804-Y30R «S 0804-Y30R»	24,6 м²

Допущения и предложения на листе. Основа листа: размеры и контуры этажей подобраны проектировщиком по составу помещений и площадям этажей с картинки 470 px (размеры на ней не читаются); обмер и исходный проект — задание (К-1); высоты: 1-й этаж 2800 мм, мансарда 2700 мм (горизонтальная часть) приняты; скаты кровли мансарды приняты по картинке: колено 1200 мм, уклон 45°, конёк вдоль длинной стороны; проект КР — задание (К-2); наружные стены 400 мм, перегородки 120 мм приняты (К-1); разрешённая мощность 15 кВт принята по типовым ТУ для частного дома (К-4); подрайон климата не задан — принят не северный (жилые от 2,5 м) (К-7). Знак «**» — предложение проектировщика, заказчиком не утверждено (согласовать с заказчиком): К-11: РО-2 — прибор под окном по оси проёма, ширина ≈ 0,7 ширины окна — предложение ОВ (лист ОВ выводил его сам до, теперь он в данных — один источник для листа, мебели, DXF и IFC); котёл и мощность не выбраны (К-11) — размер по теплотехническому расчёту. См. лист открытых вопросов (лист 8, записи К-1, К-2, К-4, К-7; лист 9, запись К-11).

Примечания

1. Развёртки — вид на стену изнутри помещения, по часовой стрелке; расположение — на схеме листа и на листе 127; размеры — в мм по чистовым поверхностям; отметки — в м от ±0,000 (чистый пол 1-го этажа); высоты H — от чистого пола помещения до оси изделия, у декора — до центра.
2. Красная цепочка — привязки электроточек и выводов по осям от угла чистовых стен; высота H — у знака, от чистого пола до оси; высоты мебели, проёмов и границ отделки — колонкой отметок слева. Стена с 5 и более точками или с мелкими звеньями привязок показана двумя видами: архитектурная развёртка (мебель, отделка, проёмы, высоты) и вид «Привязки» на отдельном листе — точки и выводы с марками, одна цепочка по осям и таблица привязок (каждая точка — строка).
3. У знака электроточки: марка (Р — розетка, S — выключатель, Св — светильник, ЭВ — вывод кабеля), ×N — число постов в рамке, гр. — группа щита, H — высота оси от чистого пола, мм; группы по клавишам выключателя — на листе выключателей.
4. Схема мебели, приборов и декора не является технической документацией для производства мебели; габариты — по паспортам изделий.
5. Потолок — у каждой стены свой, по плану потолков (НШ1, ПТ3); ступени — зоной, кромка короба перед нишей — тонкой линией; в поле потолка: ПТ1 +2,550, ПТ2 +2,600.

1000 мм · печать 1:1

Изм.	Кол.уч	Лист	№ док.	Подп.	Дата
Разраб.		Кырлан А.С.			04.11.26
Пров.					
ГИП					
Н. контр.					
Утв.					

ГД-2026-010-АИ

Дом 331 м²

Общая площадь 270,67* м² · * размеры приняты, не замерены (реестр — л. 8–10, К-1)

Дизайн-проект интерьера

Стадия	Лист	Листов
РП	133	216

Развёртка стены Г. Кухня-столовая (пом. 1)

М 1:20

Кырлан Александр Сергеевич

выпуск 04.11.2026 № 2a77323a49 · стр. 137 из 221

Развёртка стены А. Кабинет-гостевая (пом. 2)

Кабинет-гостевая (пом. 2) · вид изнутри помещения · размеры в мм, отметки в м от ±0,000 (чистый пол 1-го этажа)

Развёртка стены А


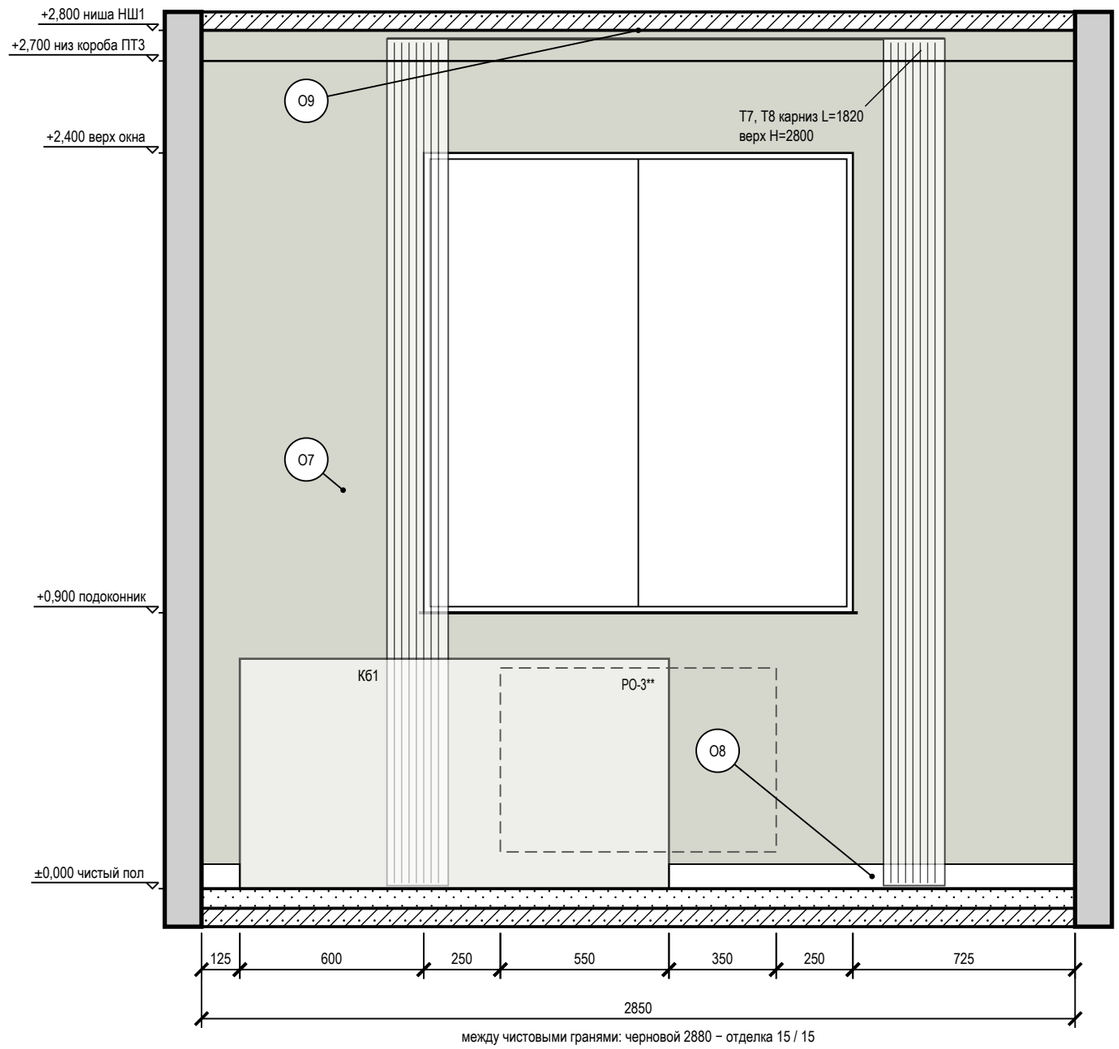


Схема развёрток (М 1:100)

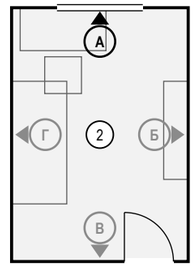

Условные обозначения

- мебель и приборы — фасад по расстановке (условно)
- карниз (шина) и шторы в собранном виде: марка Т, длина L, верх H
- окно: проём, рама, подоконник
- радиатор отопления; марка — по плану отопления
- стены и перекрытия в сечении
- окраска: тон — цвет по коду производителя (условно)
- О1 — марка отделки по реестру отделки альбома
- А — марка развёртки: буква стены, стрелка — взгляд

Ведомость отделки (на листе)

Марка	Поверхность	Материал, изделие	Цвет, код	Кол.
О7	акцентная стена	окраска, Farrow & Ball Modern Emulsion, матовая, подготовка Q3	Farrow & Ball No. 298 «Bancha»	5,9 м²
О8	плинтус	плинтус МДФ, h 80 мм, аналог: плинтус МДФ под покраску 80×16	Farrow & Ball No. 226 «Joa's White»	1,4 м
О9	потолок	окраска, Little Greene Absolute Matt, глубокоматовая, подготовка Q3	Little Greene No. 105 «Slaked Lime»	11,9 м²

Допущения и предложения на листе

Основа листа: размеры и контуры этажей подобраны проектировщиком по составу помещений и площадям этажей с картинки 470 px (размеры на ней не читаются); обмер и исходный проект — задание (К-1); высоты: 1-й этаж 2800 мм, мансарда 2700 мм (горизонтальная часть) приняты; скаты кровли мансарды приняты по картинке: колено 1200 мм, уклон 45°, конёк вдоль длинной стороны; проект КР — задание (К-2); наружные стены 400 мм, перегородки 120 мм приняты (К-1); разрешённая мощность 15 кВт принята по типовым ТУ для частного дома (К-4); подрайон климата не задан — принят не северный (жилые от 2,5 м) (К-7).

Знак «**» — предложение проектировщика, заказчиком не утверждено (согласовать с заказчиком): К-11: РО-3 — прибор под окном по оси проёма, ширина ≈ 0,7 ширины окна — предложение ОВ (лист ОВ выводил его сам до, теперь он в данных — один источник для листа, мебели, DXF и IFC); котёл и мощность не выбраны (К-11) — размер по теплотехническому расчёту.

См. лист открытых вопросов (лист 8, записи К-1, К-2, К-4, К-7; лист 9, запись К-11).

Примечания

1. Развёртки — вид на стену изнутри помещения, по часовой стрелке; расположение — на схеме листа и на листе 127; размеры — в мм по чистовым поверхностям; отметки — в м от ±0,000 (чистый пол 1-го этажа); высоты H — от чистого пола помещения до оси изделия, у декора — до центра.
2. Стена А показана двумя видами: здесь — архитектурная развёртка (мебель, отделка, проёмы, высоты), электроточки и выводы ВК с привязками и таблицей — на листе 135 («Привязки»).
3. Схема мебели, приборов и декора не является технической документацией для производства мебели; габариты — по паспортам изделий.
4. Карнизы (шины) — по ведомости текстиля декоратора: длина L и верх H на развёртке — те же числа, что в ведомости; крепление — до окраски потолка.
5. Потолок — у каждой стены свой, по плану потолков (НШ1, ПТ3); ступени — зоной, кромка короба перед нишей — тонкой линией; в поле потолка: ПТ2 +2,600.

1000 мм · печать 1:1

Изм.	Кол.уч	Лист	№ док.	Подп.	Дата
Разраб.		Кырлан А.С.			04.11.26
Пров.					
ГИП					
Н. контр.					
Утв.					

ГД-2026-010-АИ

Дом 331 м²

Общая площадь 270,67* м² · * размеры приняты, не замерены (реестр — л. 8–10, К-1)

Дизайн-проект интерьера	Стадия	Лист	Листов
	РП	134	216

Развёртка стены А. Кабинет-гостевая (пом. 2)

М 1:20

Кырлан Александр Сергеевич

выпуск 04.11.2026 № 2a77323a49 · стр. 138 из 221

Привязки электроточек, стена А. Кабинет-гостевая (пом. 2)

Кабинет-гостевая (пом. 2) · вид изнутри помещения · привязки в мм, отметки в м · к развёртке на листе 134

Развёртка стены А: электроточки и выводы

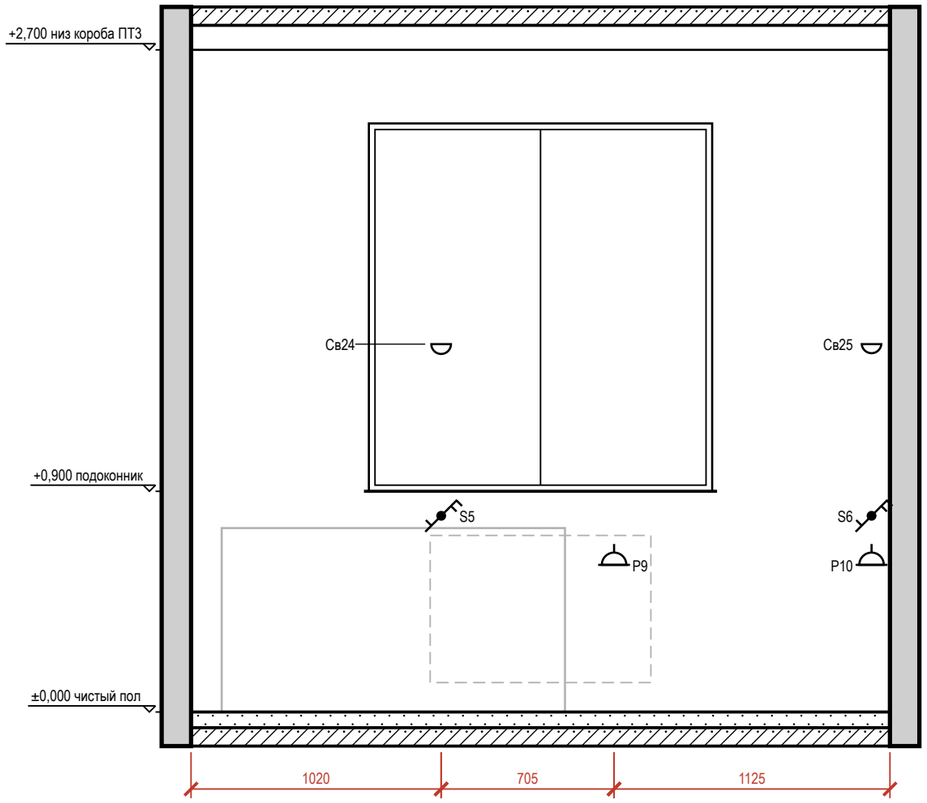



Таблица привязок электроточек и выводов

Марка	Назначение	От угла, мм	Н от пола, мм	Примечание
S5	выключатель	1020	800	гр. 1
Св24	светильник настенный	1020	1500	гр. 1
P9	розетка: у кровати	1725	600	гр. 7
P10	розетка: у кровати	2775	600	гр. 7
S6	выключатель	2775	800	гр. 1
Св25	светильник настенный	2775	1500	гр. 1

Условные обозначения

- розетка с заземляющим контактом; у знака — марка, ×N постов в рамке, гр. — группа щита, Н — высота оси, мм
- выключатель одноклавишный
- выключатель двухклавишный (флажков — по числу клавиш)
- выключатель с проходной или перекрёстной клавишей (обратный флажок); тип клавиши — в подписи
- светильник настенный (бра), Н — высота оси
- привязки точек и выводов от угла и от пола, мм
- марка развёртки: буква стены, стрелка — взгляд

Схема развёрток (М 1:100)

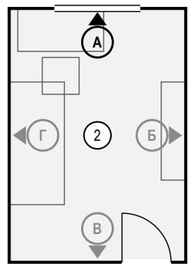

Примечания

1. Вид «Привязки» стены А — электроточки и выводы ВК; архитектурная развёртка (мебель, отделка, проёмы, высоты) — на листе 134, расположение — на листе 127. Мебель и приборы — подложкой для ориентира; их марки и обозначения мебели, проёмов и стен — там же.
2. Привязки — в мм: по горизонтали от левого чистового угла стены до оси изделия, Н — от чистого пола до оси; все точки — в таблице привязок. Красная цепочка — привязки по осям; точки ближе 150 мм одна к другой в цепочку не дробятся — их привязки только в таблице.
3. У знака — марка электроточки (Р — розетка, S — выключатель, Св — светильник, ЭВ — вывод кабеля); посты в рамке и группа щита — в графе «Примечание»; группы по клавишам выключателя — на листе выключателей.

Допущения и предложения на листе

Основа листа: размеры и контуры этажей подобраны проектировщиком по составу помещений и площадям этажей с картинки 470 px (размеры на ней не читаются); обмер и исходный проект — задание (К-1); высоты: 1-й этаж 2800 мм, мансарда 2700 мм (горизонтальная часть) приняты; скаты кровли мансарды приняты по картинке: колено 1200 мм, уклон 45°, конёк вдоль длинной стороны; проект КР — задание (К-2); наружные стены 400 мм, перегородки 120 мм приняты (К-1); разрешённая мощность 15 кВт принята по типовым ТУ для частного дома (К-4); подрайон климата не задан — принят не северный (жилые от 2,5 м) (К-7).

См. лист открытых вопросов (лист 8, записи К-1, К-2, К-4, К-7).

1000 мм · печать 1:1

Изм.	Кол.уч	Лист	№ док.	Подп.	Дата
Разраб.		Кырлан А.С.			04.11.26
Пров.					
ГИП					
Н. контр.					
Утв.					

ГД-2026-010-АИ

Дом 331 м²

Общая площадь 270,67* м² · * размеры приняты, не замерены (реестр — л. 8–10, К-1)

Дизайн-проект интерьера

Стадия	Лист	Листов
РП	135	216

Привязки электроточек, стена А.
Кабинет-гостевая (пом. 2)
М 1:25

Кырлан Александр Сергеевич

выпуск 04.11.2026 № 2a77323a49 · стр. 139 из 221

Развёртка стены Б. Кабинет-гостевая (пом. 2)

Кабинет-гостевая (пом. 2) · вид изнутри помещения · размеры в мм, отметки в м от ±0,000 (чистый пол 1-го этажа)

ПРЕДВАРИТЕЛЬНО · не для производства работ · открыто пунктов: 15 (реестр — л. 8–10)

Развёртка стены Б


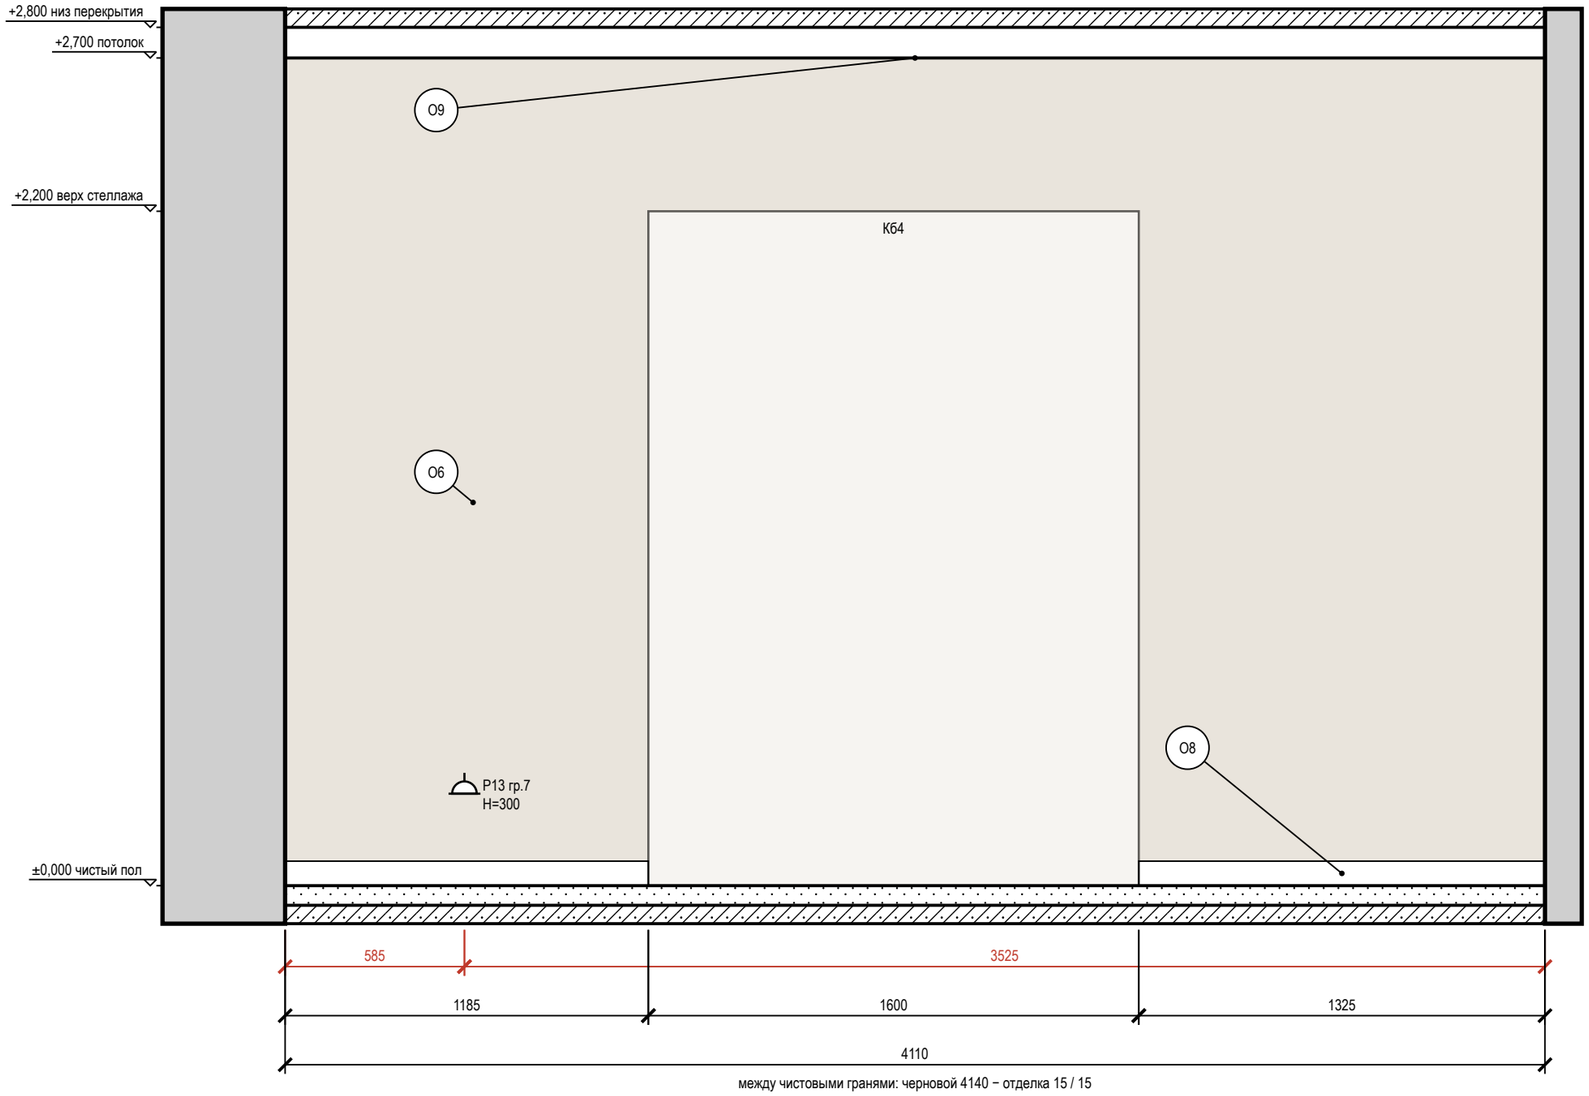


Схема развёрток (М 1:100)

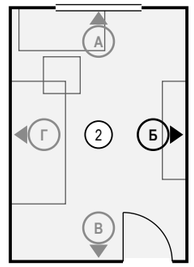

Условные обозначения

- розетка с заземляющим контактом; у знака — марка, ×N постов в рамке, гр. — группа щита, Н — высота оси, мм
- привязки точек и выводов от угла и от пола, мм
- мебель и приборы — фасад по расстановке (условно)
- стены и перекрытия в сечении
- окраска: тон — цвет по коду производителя (условно)
- О1 — марка отделки по реестру отделки альбома
- А — марка развёртки: буква стены, стрелка — взгляд

Ведомость отделки (на листе)

Марка	Поверхность	Материал, изделие	Цвет, код	Кол.
О6	стены	окраска, Farrow & Ball Modern Emulsion, матовая, подготовка Q3	Farrow & Ball No. 226 «Joa's White»	11,1 м²
О8	плинтус	плинтус МДФ, h 80 мм, аналог: плинтус МДФ под покраску 80×16	Farrow & Ball No. 226 «Joa's White»	2,5 м
О9	потолок	окраска, Little Greene Absolute Matt, глубокоматовая, подготовка Q3	Little Greene No. 105 «Slaked Lime»	11,9 м²

Допущения и предложения на листе

Основа листа: размеры и контуры этажей подобраны проектировщиком по составу помещений и площадям этажей с картинки 470 px (размеры на ней не читаются); обмер и исходный проект — задание (К-1); высоты: 1-й этаж 2800 мм, мансарда 2700 мм (горизонтальная часть) приняты; скаты кровли мансарды приняты по картинке: колено 1200 мм, уклон 45°, конёк вдоль длинной стороны; проект КР — задание (К-2); наружные стены 400 мм, перегородки 120 мм приняты (К-1); разрешённая мощность 15 кВт принята по типовым ТУ для частного дома (К-4); подрайон климата не задан — принят не северный (жилые от 2,5 м) (К-7).

См. лист открытых вопросов (лист 8, записи К-1, К-2, К-4, К-7).

Примечания

1. Развёртки — вид на стену изнутри помещения, по часовой стрелке; расположение — на схеме листа и на листе 127; размеры — в мм по чистовым поверхностям; отметки — в м от ±0,000 (чистый пол 1-го этажа); высоты Н — от чистого пола помещения до оси изделия, у декора — до центра.
2. Красная цепочка — привязки электроточек и выводов по осям от угла чистовых стен; высота Н — у знака, от чистого пола до оси; высоты мебели, проёмов и границ отделки — колонкой отметок слева. Стена с 5 и более точками или с мелкими звеньями привязок показана двумя видами: архитектурная развёртка (мебель, отделка, проёмы, высоты) и вид «Привязки» на отдельном листе — точки и выводы с марками, одна цепочка по осям и таблица привязок (каждая точка — строка).
3. У знака электроточки: марка (Р — розетка, S — выключатель, Св — светильник, ЭВ — вывод кабеля), ×N — число постов в рамке, гр. — группа щита, Н — высота оси от чистого пола, мм; группы по клавишам выключателя — на листе выключателей.
4. Схема мебели, приборов и декора не является технической документацией для производства мебели; габариты — по паспортам изделий.
5. Потолок — у каждой стены свой, по плану потолков (ПТ3); ступени — зоной, кромка короба перед нишей — тонкой линией; в поле потолка: ПТ2 +2,600.

1000 мм · печать 1:1

Изм.	Кол.уч	Лист	№ док.	Подп.	Дата
Разраб.		Кырлан А.С.			04.11.26
Пров.					
ГИП					
Н. контр.					
Утв.					

ГД-2026-010-АИ

Дом 331 м²

Общая площадь 270,67* м² · * размеры приняты, не замерены (реестр — л. 8–10, К-1)

Дизайн-проект интерьера

Стадия	Лист	Листов
РП	136	216

Развёртка стены Б. Кабинет-гостевая (пом. 2)

М 1:20


Кырлан Александр Сергеевич

выпуск 04.11.2026 № 2a77323a49 · стр. 140 из 221

Развёртка стены В. Кабинет-гостевая (пом. 2)


Кабинет-гостевая (пом. 2) · вид изнутри помещения · размеры в мм, отметки в м от ±0,000 (чистый пол 1-го этажа)

Развёртка стены В

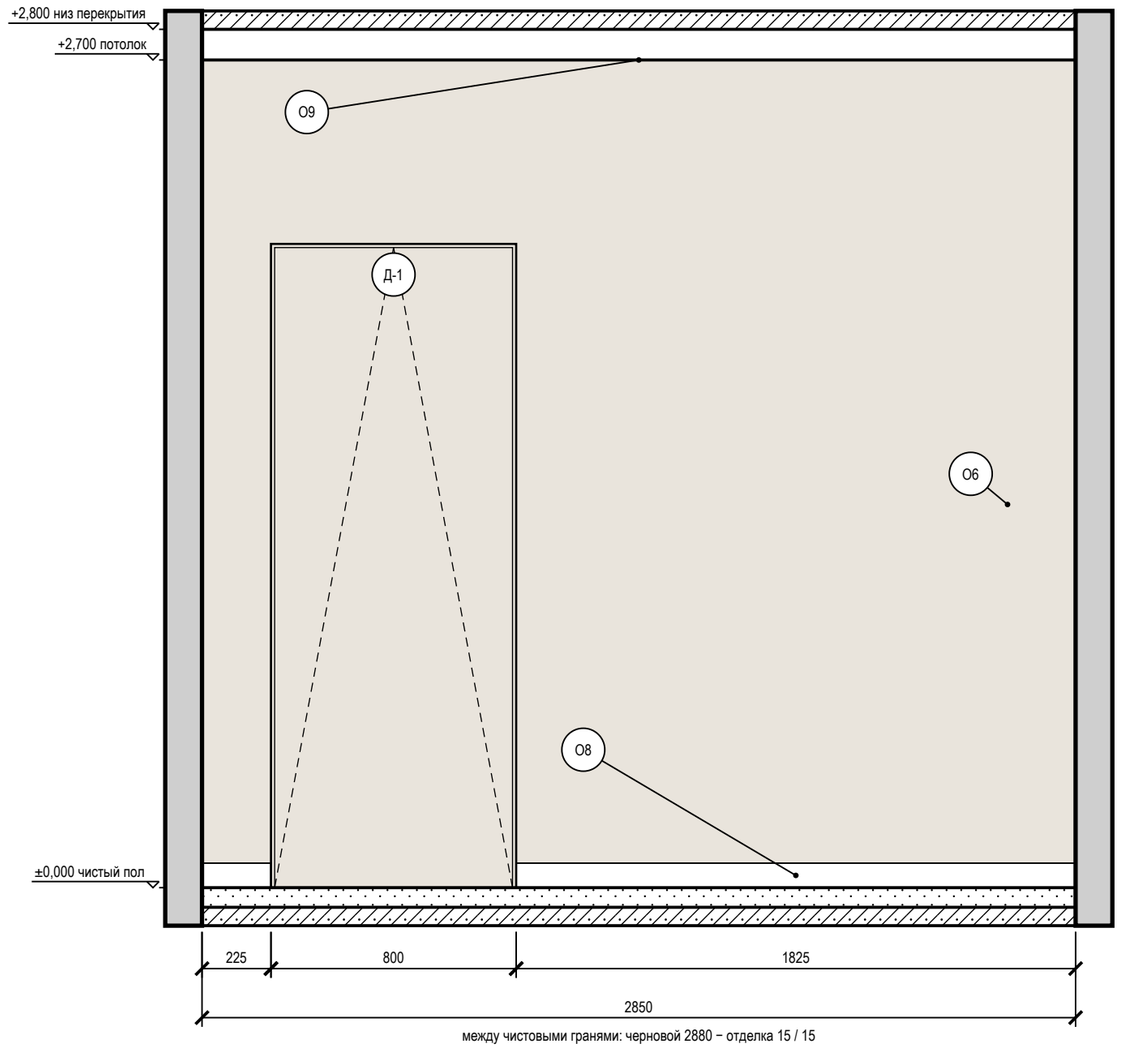

между чистовыми гранями: черновой 2880 − отделка 15 / 15

Схема развёрток (М 1:100)

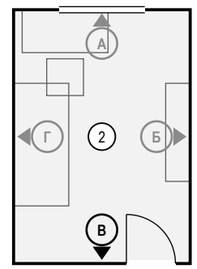

Условные обозначения

- мебель и приборы — фасад по расстановке (условно)
- дверь скрытого монтажа: полотно в плоскости стены (узел — на листе узлов)
- стены и перекрытия в сечении
- окраска: тон — цвет по коду производителя (условно)
- О1 — марка отделки по реестру отделки альбома
- А — марка развёртки: буква стены, стрелка — взгляд

Ведомость отделки (на листе)

Марка	Поверхность	Материал, изделие	Цвет, код	Кол.
О6	стены	окраска, Farrow & Ball Modern Emulsion, матовая, подготовка Q3	Farrow & Ball No. 226 «Joa's White»	6 м²
О8	плинтус	плинтус МДФ, h 80 мм, аналог: плинтус МДФ под покраску 80×16	Farrow & Ball No. 226 «Joa's White»	2 м
О9	потолок	окраска, Little Greene Absolute Matt, глубокоматовая, подготовка Q3	Little Greene No. 105 «Slaked Lime»	11,9 м²

Допущения и предложения на листе

Основа листа: размеры и контуры этажей подобраны проектировщиком по составу помещений и площадям этажей с картинки 470 px (размеры на ней не читаются); обмер и исходный проект — задание (К-1); высоты: 1-й этаж 2800 мм, мансарда 2700 мм (горизонтальная часть) приняты; скаты кровли мансарды приняты по картинке: колено 1200 мм, уклон 45°, конёк вдоль длинной стороны; проект КР — задание (К-2); наружные стены 400 мм, перегородки 120 мм приняты (К-1); разрешённая мощность 15 кВт принята по типовым ТУ для частного дома (К-4); подрайон климата не задан — принят не северный (жилые от 2,5 м) (К-7).

См. лист открытых вопросов (лист 8, записи К-1, К-2, К-4, К-7).

Примечания

1. Развёртки — вид на стену изнутри помещения, по часовой стрелке; расположение — на схеме листа и на листе 127; размеры — в мм по чистовым поверхностям; отметки — в м от ±0,000 (чистый пол 1-го этажа); высоты Н — от чистого пола помещения до оси изделия, у декора — до центра.
2. Стена В показана двумя видами: здесь — архитектурная развёртка (мебель, отделка, проёмы, высоты), электроточки и выводы ВК с привязками и таблицей — на листе 138 («Привязки»).
3. Схема мебели, приборов и декора не является технической документацией для производства мебели; габариты — по паспортам изделий.
4. Двери скрытого монтажа — полотно в плоскости стены, отделка стены по полотну, плинтус прерывается у короба (узел — на листе узлов).
5. Потолок — у каждой стены свой, по плану потолков (ПТ3); ступени — зоной, кромка короба перед нишей — тонкой линией; в поле потолка: ПТ2 +2,600.

1000 мм · печать 1:1

Изм.	Кол.уч	Лист	№ док.	Подп.	Дата
Разраб.		Кырлан А.С.			04.11.26
Пров.					
ГИП					
Н. контр.					
Утв.					

ГД-2026-010-АИ

Дом 331 м²

Общая площадь 270,67* м² · * размеры приняты, не замерены (реестр — л. 8–10, К-1)

Дизайн-проект интерьера

Стадия	Лист	Листов
РП	137	216

Развёртка стены В. Кабинет-гостевая (пом. 2)

М 1:20

Кырлан Александр Сергеевич

выпуск 04.11.2026 № 2a77323a49 · стр. 141 из 221

Привязки электроточек, стена В. Кабинет-гостевая (пом. 2)

Кабинет-гостевая (пом. 2) · вид изнутри помещения · привязки в мм, отметки в м · к развёртке на листе 137

Развёртка стены В: электроточки и выводы

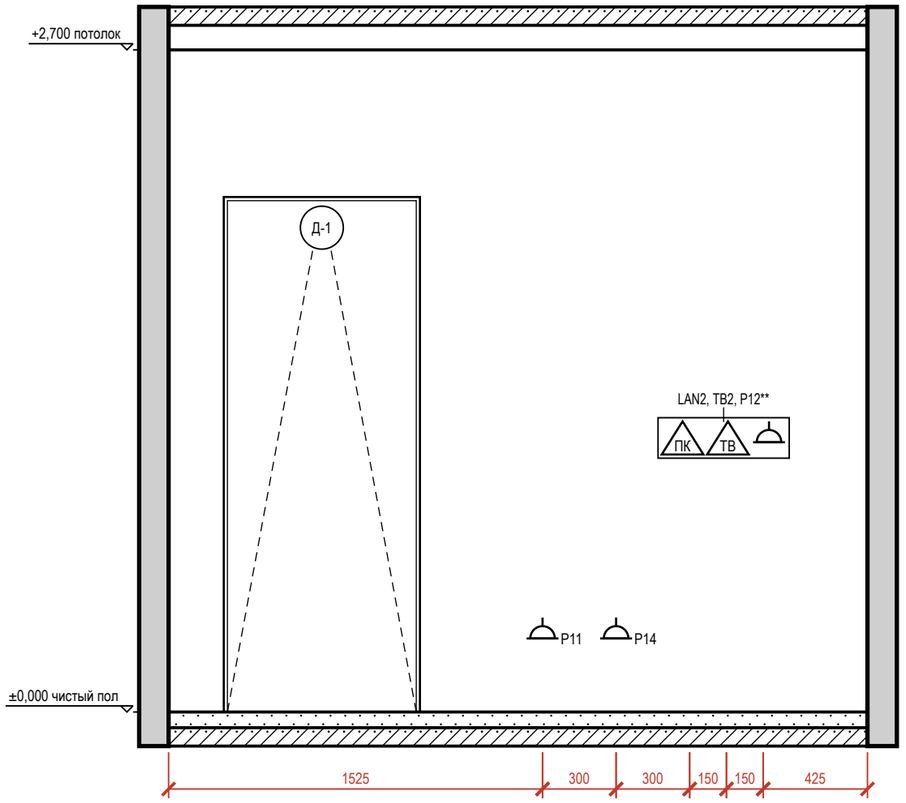



Таблица привязок электроточек и выводов

Марка	Назначение	От угла, мм	Н от пола, мм	Примечание
Р11	розетка: у комода	1525	300	гр. 7
Р14	розетка: уборка у входа	1825	300	гр. 7
LAN2	розетка RJ45: Smart TV	2125	1100	
ТВ2	розетка ТВ: ТВ над комодом	2275	1100	
Р12**	розетка: ТВ над комодом (в одной зоне с ТВ2, LAN2)	2425	1100	гр. 7

Условные обозначения

- розетка с заземляющим контактом; у знака — марка, ×N постов в рамке, гр. — группа щита, Н — высота оси, мм
- ПК — розетка компьютерная RJ45
- ТВ — розетка телевизионная
- привязки точек и выводов от угла и от пола, мм
- А — марка развёртки: буква стены, стрелка — взгляд

Схема развёрток (М 1:100)

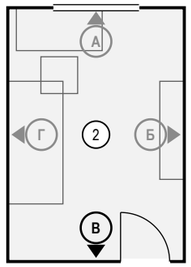

Примечания

1. Вид «Привязки» стены В — электроточки и выводы ВК; архитектурная развёртка (мебель, отделка, проёмы, высоты) — на листе 137, расположение — на листе 127. Мебель и приборы — подложкой для ориентира; их марки и обозначения мебели, проёмов и стен — там же.
2. Привязки — в мм: по горизонтали от левого чистового угла стены до оси изделия, Н — от чистого пола до оси; все точки — в таблице привязок. Красная цепочка — привязки по осям; точки ближе 150 мм одна к другой в цепочку не дробятся — их привязки только в таблице.
3. У знака — марка электроточки (Р — розетка, S — выключатель, Св — светильник, ЭВ — вывод кабеля); посты в рамке и группа щита — в графе «Примечание»; группы по клавишам выключателя — на листе выключателей.

Допущения и предложения на листе

Основа листа: размеры и контуры этажей подобраны проектировщиком по составу помещений и площадям этажей с картинки 470 px (размеры на ней не читаются); обмер и исходный проект — задание (К-1); высоты: 1-й этаж 2800 мм, мансарда 2700 мм (горизонтальная часть) приняты; скаты кровли мансарды приняты по картинке: колено 1200 мм, уклон 45°, конёк вдоль длинной стороны; проект КР — задание (К-2); наружные стены 400 мм, перегородки 120 мм приняты (К-1); разрешённая мощность 15 кВт принята по типовым ТУ для частного дома (К-4); подрайон климата не задан — принят не северный (жилые от 2,5 м) (К-7).

Знак «**» — предложение проектировщика, заказчиком не утверждено (согласовать с заказчиком): Р12 — высота 1100 мм выше нормы 1 м (ПУЭ 6.6.30) по назначению: питание ТВ над комодом, в одной зоне с выводами ТВ2 и LAN2.

См. лист открытых вопросов (лист 8, записи К-1, К-2, К-4, К-7).

1000 мм · печать 1:1

Изм.	Кол.уч	Лист	№ док.	Подп.	Дата
Разраб.		Кырлан А.С.			04.11.26
Пров.					
ГИП					
Н. контр.					
Утв.					

ГД-2026-010-АИ

Дом 331 м²

Общая площадь 270,67* м² · * размеры приняты, не замерены (реестр — л. 8–10, К-1)

Дизайн-проект интерьера	Стадия	Лист	Листов
	РП	138	216

Привязки электроточек, стена В.
Кабинет-гостевая (пом. 2)
М 1:25

Кырлан Александр Сергеевич

выпуск 04.11.2026 № 2a77323a49 · стр. 142 из 221

Развёртка стены Г. Кабинет-гостевая (пом. 2)

Кабинет-гостевая (пом. 2) · вид изнутри помещения · размеры в мм, отметки в м от ±0,000 (чистый пол 1-го этажа)

ПРЕДВАРИТЕЛЬНО · не для производства работ · открыто пунктов: 15 (реестр — л. 8–10)

Развёртка стены Г


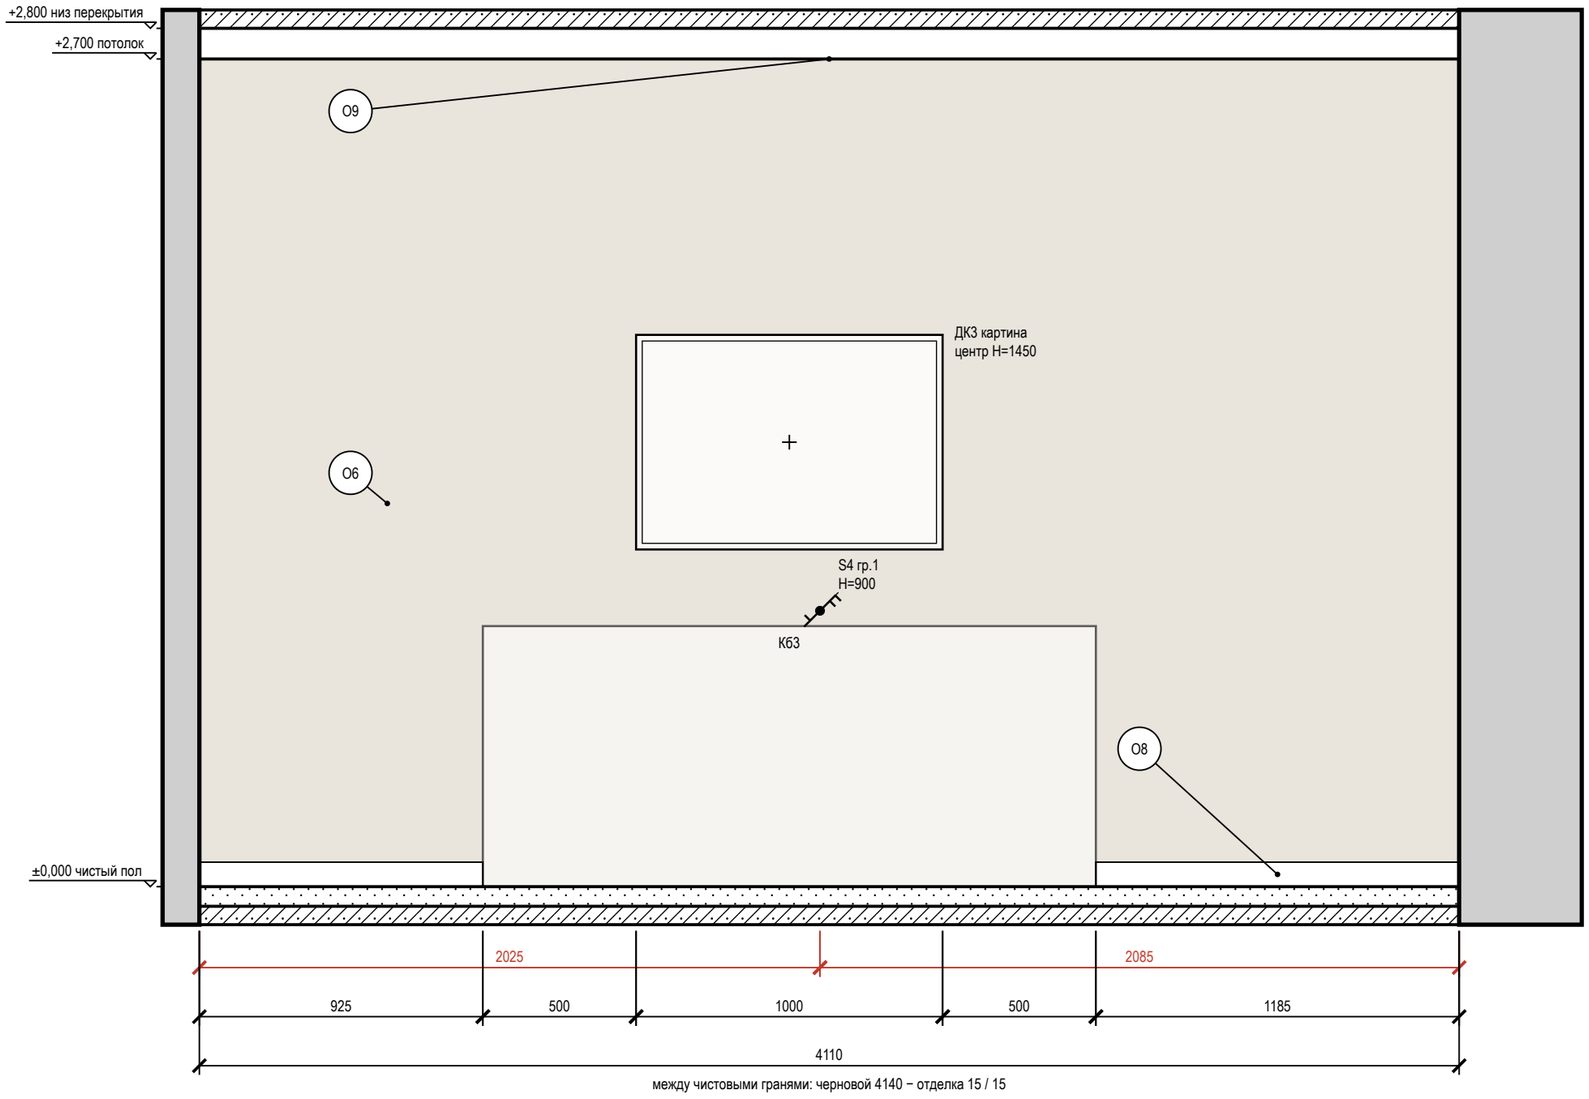


Схема развёрток (М 1:100)

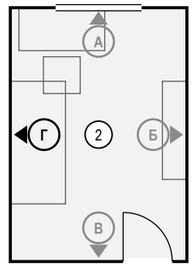

Условные обозначения

- выключатель одноклавишный
- выключатель двухклавишный (флажков — по числу клавиш)
- выключатель с проходной или перекрёстной клавишей (обратный флажок); тип клавиши — в подписи
- привязки точек и выводов от угла и от пола, мм
- мебель и приборы — фасад по расстановке (условно)
- картина (декор): марка Д, крест — центр, Н — высота центра, мм
- стены и перекрытия в сечении
- окраска: тон — цвет по коду производителя (условно)
- О1 — марка отделки по реестру отделки альбома
- А — марка развёртки: буква стены, стрелка — взгляд

Ведомость отделки (на листе)

Марка	Поверхность	Материал, изделие	Цвет, код	Кол.
О6	стены	окраска, Farrow & Ball Modern Emulsion, матовая, подготовка Q3	Farrow & Ball No. 226 «Joa's White»	11,1 м²
О8	плинтус	плинтус МДФ, h 80 мм, аналог: плинтус МДФ под покраску 80×16	Farrow & Ball No. 226 «Joa's White»	2,1 м
О9	потолок	окраска, Little Greene Absolute Matt, глубокоматовая, подготовка Q3	Little Greene No. 105 «Slaked Lime»	11,9 м²

Допущения и предложения на листе

Основа листа: размеры и контуры этажей подобраны проектировщиком по составу помещений и площадям этажей с картинки 470 px (размеры на ней не читаются); обмер и исходный проект — задание (К-1); высоты: 1-й этаж 2800 мм, мансарда 2700 мм (горизонтальная часть) приняты; скаты кровли мансарды приняты по картинке: колено 1200 мм, уклон 45°, конёк вдоль длинной стороны; проект КР — задание (К-2); наружные стены 400 мм, перегородки 120 мм приняты (К-1); разрешённая мощность 15 кВт принята по типовым ТУ для частного дома (К-4); подрайон климата не задан — принят не северный (жилые от 2,5 м) (К-7).

См. лист открытых вопросов (лист 8, записи К-1, К-2, К-4, К-7).

Примечания

1. Развёртки — вид на стену изнутри помещения, по часовой стрелке; расположение — на схеме листа и на листе 127; размеры — в мм по чистовым поверхностям; отметки — в м от ±0,000 (чистый пол 1-го этажа); высоты Н — от чистого пола помещения до оси изделия, у декора — до центра.
2. Красная цепочка — привязки электроточек и выводов по осям от угла чистовых стен; высота Н — у знака, от чистого пола до оси; высоты мебели, проёмов и границ отделки — колонкой отметок слева. Стена с 5 и более точками или с мелкими звеньями привязок показана двумя видами: архитектурная развёртка (мебель, отделка, проёмы, высоты) и вид «Привязки» на отдельном листе — точки и выводы с марками, одна цепочка по осям и таблица привязок (каждая точка — строка).
3. У знака электроточки: марка (Р — розетка, S — выключатель, Св — светильник, ЭВ — вывод кабеля), ×N — число постов в рамке, гр. — группа щита, Н — высота оси от чистого пола, мм; группы по клавишам выключателя — на листе выключателей.
4. Схема мебели, приборов и декора не является технической документацией для производства мебели; габариты — по паспортам изделий.
5. Картины и зеркала крепить к основанию по паспорту изделия (закладные и анкеры — в перечне скрытых работ); крест — ось центра предмета.
6. Потолок — у каждой стены свой, по плану потолков (ПТ3); ступени — зоной, кромка короба перед нишей — тонкой линией; в поле потолка: ПТ2 +2,600.

1000 мм · печать 1:1

Изм.	Кол.уч	Лист	№ док.	Подп.	Дата
Разраб.		Кырлан А.С.			04.11.26
Пров.					
ГИП					
Н. контр.					
Утв.					

ГД-2026-010-АИ

Дом 331 м²

Общая площадь 270,67* м² · * размеры приняты, не замерены (реестр — л. 8–10, К-1)

Дизайн-проект интерьера	Стадия	Лист	Листов
	РП	139	216

Развёртка стены Г. Кабинет-гостевая (пом. 2)

М 1:20

Кырлан Александр Сергеевич


выпуск 04.11.2026 № 2a77323a49 · стр. 143 из 221

Развёртки стен А, Б. Санузел 1 этажа (пом. 3)

Санузел 1 этажа (пом. 3) · вид изнутри помещения · размеры в мм, отметки в м от ±0,000 (чистый пол 1-го этажа)


ПРЕДВАРИТЕЛЬНО · не для производства работ · открыто пунктов: 15 (реестр — л. 8–10)

Развёртка стены А

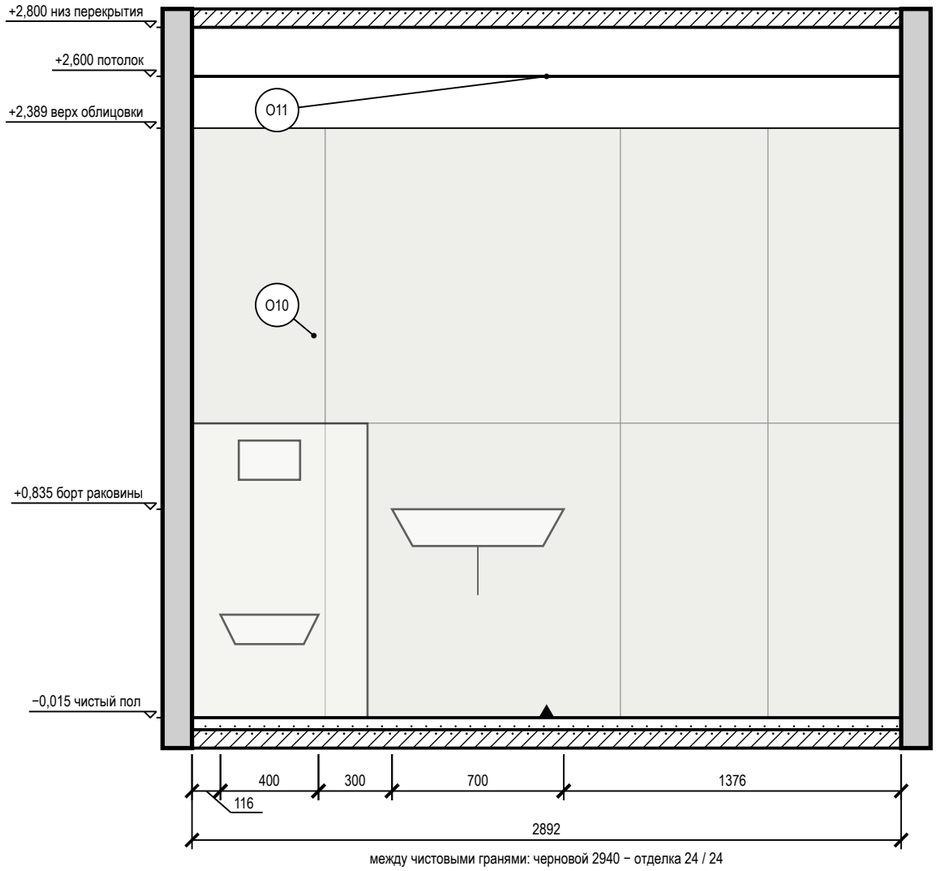


между чистовыми гранями: черновой 2940 − отделка 24 / 24

Развёртка стены Б

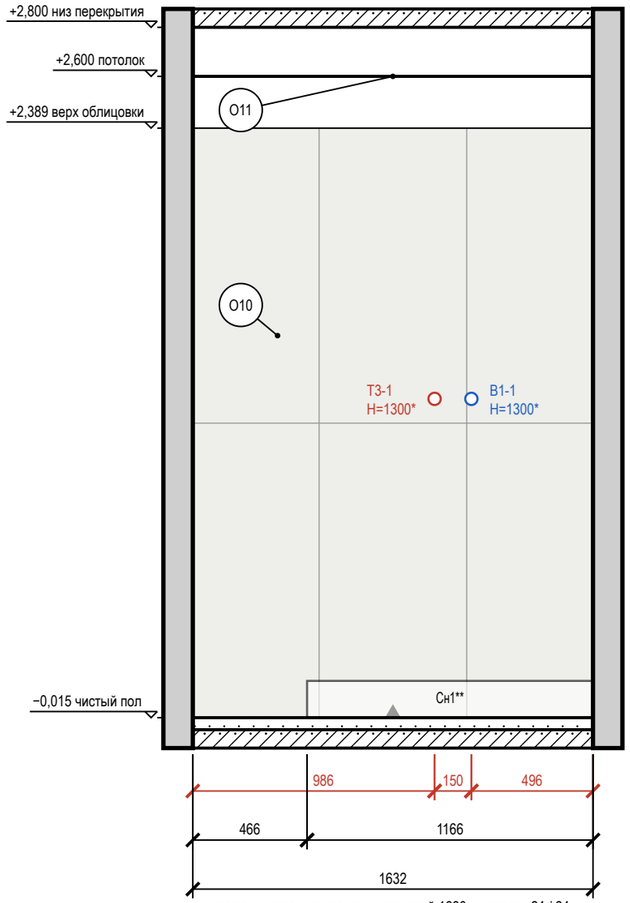

между чистовыми гранями: черновой 1680 − отделка 24 / 24

Схема развёрток (М 1:100)

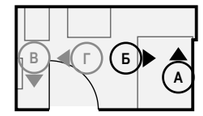

Условные обозначения

- вывод В1 (код — в ведомости привязок)
- вывод Т3 (код — в ведомости привязок)
- привязки точек и выводов от угла и от пола, мм
- мебель и приборы — фасад по расстановке (условно)
- стены и перекрытия в сечении
- плитка: сетка швов по формату, ▲ — ось старта
- О1 — марка отделки по реестру отделки альбома
- А — марка развёртки: буква стены, стрелка — взгляд

Ведомость отделки (на листе)

Марка	Поверхность	Материал, изделие	Цвет, код	Кол.
О10	стены	облицовка плиткой, Atlas Concorde Marvel Travertine, 600×1200×9 мм, А8UZ, затирка CG2WA	Atlas Concorde A8UZ «Marvel Travertine»	10,9 м²
О11	потолок	окраска, Little Greene Intelligent Bathroom, матовая, подготовка Q3	Little Greene No. 105 «Slaked Lime»	4,9 м²

Допущения и предложения на листе

Основа листа: размеры и контуры этажей подобраны проектировщиком по составу помещений и площадям этажей с картинки 470 px (размеры на ней не читаются); обмер и исходный проект — задание (К-1); высоты: 1-й этаж 2800 мм, мансарда 2700 мм (горизонтальная часть) приняты; скаты кровли мансарды приняты по картинке: колено 1200 мм, уклон 45°, конёк вдоль длинной стороны; проект КР — задание (К-2); наружные стены 400 мм, перегородки 120 мм приняты (К-1); разрешённая мощность 15 кВт принята по типовым ТУ для частного дома (К-4); подрайон климата не задан — принят не северный (жилые от 2,5 м) (К-7).

Знак «**» — предложение проектировщика, заказчиком не утверждено (согласовать с заказчиком): К-8: Сн1 — Подиум душевой зоны 100 мм — предложение проектировщика: трап в стяжке 35 мм не встаёт (монтажная высота трапа 90 + уклон отвода до стояка 42 = 132 мм).

См. лист открытых вопросов (лист 8, записи К-1, К-2, К-4, К-7; лист 9, запись К-8).

Примечания

1. Развёртки — вид на стену изнутри помещения, по часовой стрелке; расположение — на схеме листа и на листе 127; размеры — в мм по чистовым поверхностям; отметки — в м от ±0,000 (чистый пол 1-го этажа); высоты Н — от чистого пола помещения до оси изделия, у декора — до центра.
2. Красная цепочка — привязки электроточек и выводов по осям от угла чистовых стен; высота Н — у знака, от чистого пола до оси; высоты мебели, проёмов и границ отделки — колонкой отметок слева. Стена с 5 и более точками или с мелкими звеньями привязок показана двумя видами: архитектурная развёртка (мебель, отделка, проёмы, высоты) и вид «Привязки» на отдельном листе — точки и выводы с марками, одна цепочка по осям и таблица привязок (каждая точка — строка).
3. Стена А показана двумя видами: здесь — архитектурная развёртка (мебель, отделка, проёмы, высоты), электроточки и выводы ВК с привязками и таблицей — на листе 141 («Привязки»).
4. У знака электроточки: марка (Р — розетка, S — выключатель, Св — светильник, ЭВ — вывод кабеля), ×N — число постов в рамке, гр. — группа щита, Н — высота оси от чистого пола, мм; группы по клавишам выключателя — на листе выключателей.
5. Схема мебели, приборов и декора не является технической документацией для производства мебели; габариты — по паспортам изделий (* — высота не задана в проекте, показана по типовому изделию).
6. Выводы ВК — коды и высоты по листу выводов сантехники; * — высота принята по типовой практике монтажа, окончательно — по паспорту прибора.
7. Облицовка — по сетке швов 2 мм, раскладка от оси стены (треугольник у пола), целые ряды от пола; подрезки — по листу раскладки плитки.
8. Гидроизоляция в 2 слоя, заход на стены 200 мм; у душа — на всю высоту стен душевой зоны и 500 мм за край душевой зоны — до облицовки, с актом скрытых работ и тестом проливом (узел — на листе узлов).

1000 мм · печать 1:1

Изм.	Кол.уч	Лист	№ док.	Подп.	Дата
Разраб.		Кырлан А.С.			04.11.26
Пров.					
ГИП					
Н. контр.					
Утв.					

ГД-2026-010-АИ

Дом 331 м²

Общая площадь 270,67* м² · * размеры приняты, не замерены (реестр — л. 8–10, К-1)

Дизайн-проект интерьера

Стадия	Лист	Листов
РП	140	216

Развёртки стен А, Б. Санузел 1 этажа (пом. 3)

М 1:25

Кырлан Александр Сергеевич

выпуск 04.11.2026 № 2a77323a49 · стр. 144 из 221

Привязки выводов ВК, стена А. Санузел 1 этажа (пом. 3)

Санузел 1 этажа (пом. 3) · вид изнутри помещения · привязки в мм, отметки в м · к развёртке на листе 140

ПРЕДВАРИТЕЛЬНО · не для производства работ · открыто пунктов: 15 (реестр — л. 8–10)

Развёртка стены А: электроточки и выводы

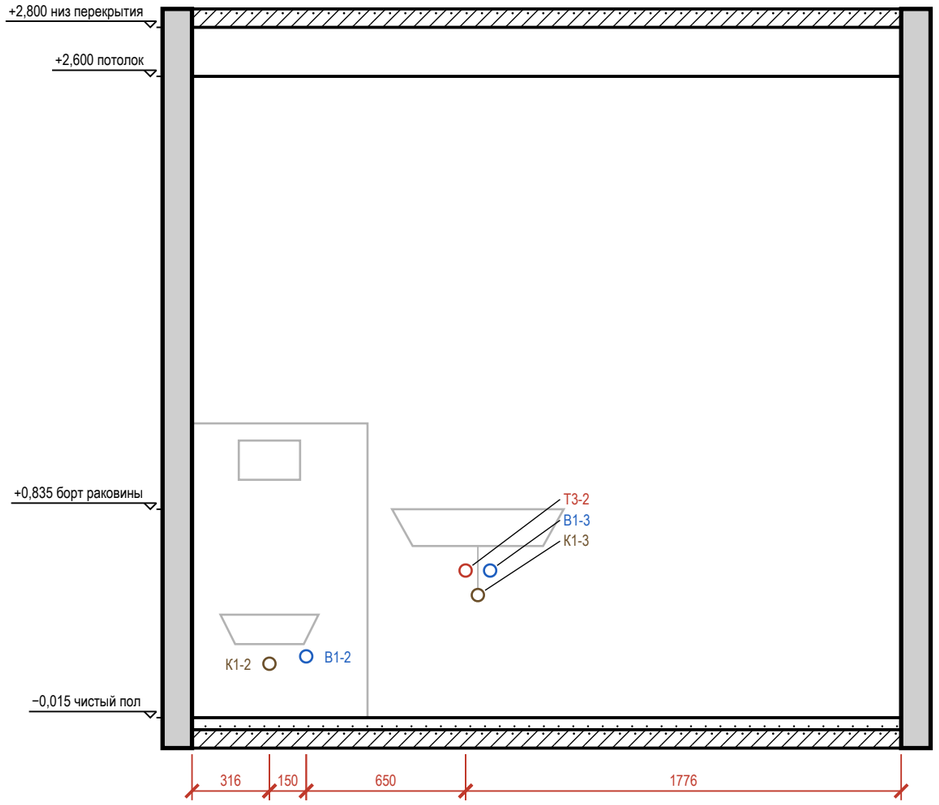



Таблица привязок электроточек и выводов

Марка	Назначение	От угла, мм	Н от пола, мм	Примечание
К1-2	канализация — унитаз подвесной	316	220*	Ø110
В1-2	холодная вода — унитаз подвесной	466	250*	в раме инсталляции
Т3-2	горячая вода — умывальник	1116	600*	межос. 100
К1-3	канализация — умывальник	1166	500*	Ø50
В1-3	холодная вода — умывальник	1216	600*	межос. 100

Условные обозначения

- вывод В1 (код — в ведомости привязок)
- вывод Т3 (код — в ведомости привязок)
- вывод К1 (код — в ведомости привязок)
- привязки точек и выводов от угла и от пола, мм
- марка развёртки: буква стены, стрелка — взгляд

Схема развёрток (М 1:50)

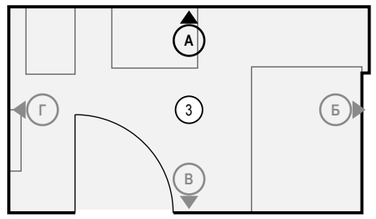

Примечания

1. Вид «Привязки» стены А — электроточки и выводы ВК; архитектурная развёртка (мебель, отделка, проёмы, высоты) — на листе 140, расположение — на листе 127. Мебель и приборы — подложкой для ориентира; их марки и обозначения мебели, проёмов и стен — там же.
2. Привязки — в мм: по горизонтали от левого чистового угла стены до оси изделия, Н — от чистого пола до оси; все точки — в таблице привязок. Красная цепочка — привязки по осям; точки ближе 150 мм одна к другой в цепочку не дробятся — их привязки только в таблице.
3. Коды выводов ВК: В1 — холодная вода, Т3 — горячая вода, К1 — канализация; номер после дефиса — номер вывода на листе выводов сантехники; * — высота принята по типовой практике монтажа, окончательно — по паспорту прибора.

Допущения и предложения на листе

Основа листа: размеры и контуры этажей подобраны проектировщиком по составу помещений и площадям этажей с картинки 470 px (размеры на ней не читаются); обмер и исходный проект — задание (К-1); высоты: 1-й этаж 2800 мм, мансарда 2700 мм (горизонтальная часть) приняты; скаты кровли мансарды приняты по картинке: колено 1200 мм, уклон 45°, конёк вдоль длинной стороны; проект КР — задание (К-2); наружные стены 400 мм, перегородки 120 мм приняты (К-1); разрешённая мощность 15 кВт принята по типовым ТУ для частного дома (К-4); подрайон климата не задан — принят не северный (жилые от 2,5 м) (К-7).

См. лист открытых вопросов (лист 8, записи К-1, К-2, К-4, К-7).

1000 мм · печать 1:1

Изм.	Кол.уч	Лист	№ док.	Подп.	Дата
Разраб.		Кырлан А.С.			04.11.26
Пров.					
ГИП					
Н. контр.					
Утв.					

ГД-2026-010-АИ

Дом 331 м²

Общая площадь 270,67* м² · * размеры приняты, не замерены (реестр — л. 8–10, К-1)

Дизайн-проект интерьера	Стадия	Лист	Листов
	РП	141	216

Привязки выводов ВК, стена А. Санузел 1 этажа (пом. 3)

М 1:25

Кырлан Александр Сергеевич


выпуск 04.11.2026 · 2a77323a49 · стр. 145 из 221

Развёртки стен В, Г. Санузел 1 этажа (пом. 3)

Санузел 1 этажа (пом. 3) · вид изнутри помещения · размеры в мм, отметки в м от ±0,000 (чистый пол 1-го этажа)


ПРЕДВАРИТЕЛЬНО · не для производства работ · открыто пунктов: 15 (реестр — л. 8–10)

Развёртка стены В

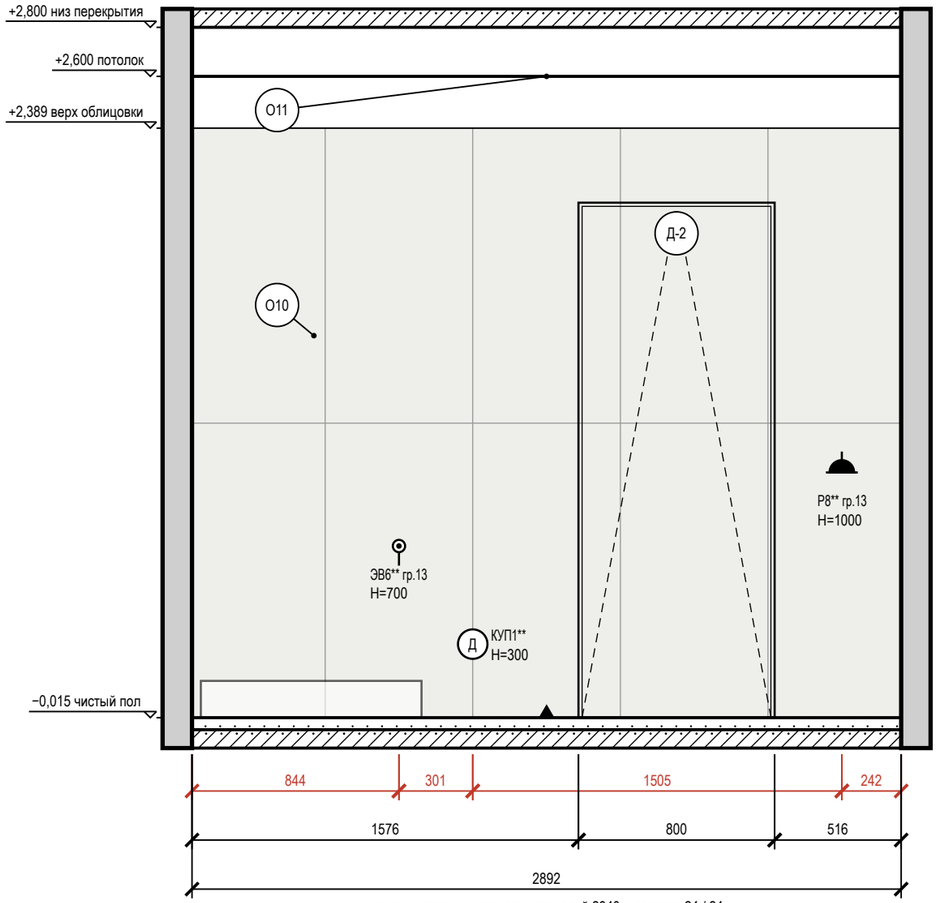


между чистовыми гранями: черновой 2940 − отделка 24 / 24

Развёртка стены Г

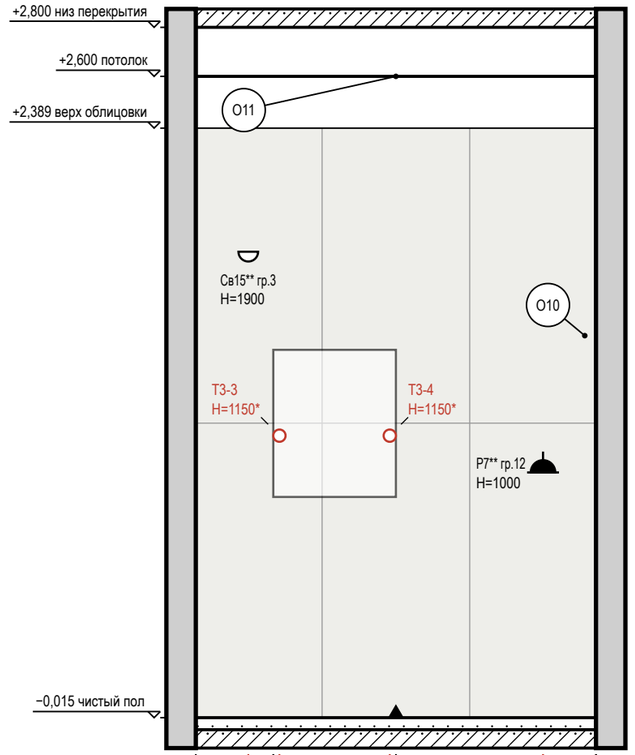

между чистовыми гранями: черновой 1680 − отделка 24 / 24

Схема развёрток (М 1:100)

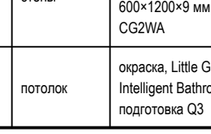

Условные обозначения

- розетка влагозащищённая IP44
- вывод кабеля для подключения прибора (без розетки), марка ЭВ
- светильник настенный (бра), Н — высота оси
- вывод Т3 (код — в ведомости привязок)
- привязки точек и выводов от угла и от пола, мм
- мебель и приборы — фасад по расстановке (условно)
- дверь скрытого монтажа: полотно в плоскости стены (узел — на листе узлов)
- стены и перекрытия в сечении
- плитка: сетка швов по формату, ▲ — ось старта
- О1 — марка отделки по реестру отделки альбома
- А — марка развёртки: буква стены, стрелка — взгляд

Ведомость отделки (на листе)

Марка	Поверхность	Материал, изделие	Цвет, код	Кол.
О10	стены	облицовка плиткой, Atlas Concorde Marvel Travertine, 600×1200×9 мм, A8UZ, затирка CG2WA	Atlas Concorde A8UZ «Marvel Travertine»	9,2 м²
О11	потолок	окраска, Little Greene Intelligent Bathroom, матовая, подготовка Q3	Little Greene No. 105 «Slaked Lime»	4,9 м²

Допущения и предложения на листе. Основа листа: размеры и контуры этажей подобраны проектировщиком по составу помещений и площадям этажей с картинки 470 px (размеры на ней не читаются); обмер и исходный проект — задание (К-1); высоты: 1-й этаж 2800 мм, мансарда 2700 мм (горизонтальная часть) приняты; скаты кровли мансарды приняты по картинке: колено 1200 мм, уклон 45°, конёк вдоль длинной стороны; проект КР — задание (К-2); наружные стены 400 мм, перегородки 120 мм приняты (К-1); разрешённая мощность 15 кВт принята по типовым ТУ для частного дома (К-4); подрайон климата не задан — принят не северный (жилые от 2,5 м) (К-7). Знак «**» — предложение проектировщика, заказчиком не утверждено (согласовать с заказчиком): Р7 — по образцу: Р7, Р8 и Р33 на высоте 1000 мм — верхний предел нормы (ПУЭ, п. 6.6.30, не выше 1 м); флаг решения снят; Р8 — по образцу: Р7, Р8 и Р33 на высоте 1000 мм — верхний предел нормы (ПУЭ, п. 6.6.30, не выше 1 м); флаг решения снят; сдвиг под раскладку плитки стены В на 26 мм вдоль стены — ось на шве или в центре плитки, привязка по таблице листа; Св15 — Сдвиг под раскладку плитки стены Г на 52 мм вдоль стены — ось на шве или в центре плитки, привязка по таблице листа; КУП1 — по образцу: Добавлены выводы к вентиляторам: ЭВ4 (ВР1, ванная) и ЭВ5 (ВР3, санузел 2) — группа 3, высота 2389 мм, включение с основным светом, таймер выбега в вентиляторе; и коробки уравнивания потенциалов КУП1 (ванная) и КУП2 (санузел 2) — высота 300 мм, у входа, вне зон 0–2, проводник от шины PE щита ЩК …; сдвиг под раскладку плитки стены В на 131 мм вдоль стены — ось на шве или в центре плитки, привязка по таблице листа; ЭВ6 — по образцу: Добавлены электрические полотенцесушители IP44: П10 в ванной (480 мм, низ 900 мм) и П13 в санузле 2 (400 мм, низ 900 мм), выводы ЭВ6 и ЭВ7; мощность группы 13 — 2,4 кВт вместо 1,8 кВт; сдвиг под раскладку плитки стены В на 127 мм вдоль стены — ось на шве или в центре плитки, привязка по таблице листа. См. лист открытых вопросов (лист 8, записи К-1, К-2, К-4, К-7).

Примечания

1. Развёртки — вид на стену изнутри помещения, по часовой стрелке; расположение — на схеме листа и на листе 127; размеры — в мм по чистовым поверхностям; отметки — в м от ±0,000 (чистый пол 1-го этажа); высоты Н — от чистого пола помещения до оси изделия, у декора — до центра.
2. Красная цепочка — привязки электроточек и выводов по осям от угла чистовых стен; высота Н — у знака, от чистого пола до оси; высоты мебели, проёмов и границ отделки — колонкой отметок слева. Стена с 5 и более точками или с мелкими звеньями привязок показана двумя видами: архитектурная развёртка (мебель, отделка, проёмы, высоты) и вид «Привязки» на отдельном листе — точки и выводы с марками, одна цепочка по осям и таблица привязок (каждая точка — строка).
3. У знака электроточки: марка (Р — розетка, S — выключатель, Св — светильник, ЭВ — вывод кабеля), ×N — число постов в рамке, гр. — группа щита, Н — высота оси от чистого пола, мм; группы по клавишам выключателя — на листе выключателей.
4. Схема мебели, приборов и декора не является технической документацией для производства мебели; габариты — по паспортам изделий (* — высота не задана в проекте, показана по типовому изделию).
5. Выводы ВК — коды и высоты по листу выводов сантехники; * — высота принята по типовой практике монтажа, окончательно — по паспорту прибора.
6. Облицовка — по сетке швов 2 мм, раскладка от оси стены (треугольник у пола), целые ряды от пола; подрезки — по листу раскладки плитки.
7. Гидроизоляция в 2 слоя, заход на стены 200 мм; у душа — на всю высоту стен душевой зоны и 500 мм за край душевой зоны — до облицовки, с актом скрытых работ и тестом проливом (узел — на листе узлов).
8. Двери скрытого монтажа — полотно в плоскости стены, отделка стены по полотну, плинтус прерывается у короба (узел — на листе узлов).

1000 мм · печать 1:1

Изм.	Кол.уч	Лист	№ док.	Подп.	Дата
Разраб.		Кырлан А.С.			04.11.26
Пров.					
ГИП					
Н. контр.					
Утв.					

ГД-2026-010-АИ

Дом 331 м²

Общая площадь 270,67* м² · * размеры приняты, не замерены (реестр — л. 8–10, К-1)

Дизайн-проект интерьера	Стадия	Лист	Листов
	РП	142	216

Развёртки стен В, Г. Санузел 1 этажа (пом. 3)

М 1:25

Кырлан Александр Сергеевич


выпуск 04.11.2026 № 2a77323a49 · стр. 146 из 221

Развёртки стен А, Б. Котельная (пом. 4)

Котельная (пом. 4) · вид изнутри помещения · размеры в мм, отметки в м от ±0,000 (чистый пол 1-го этажа)


ПРЕДВАРИТЕЛЬНО · не для производства работ · открыто пунктов: 15 (реестр — л. 8–10)

Развёртка стены А

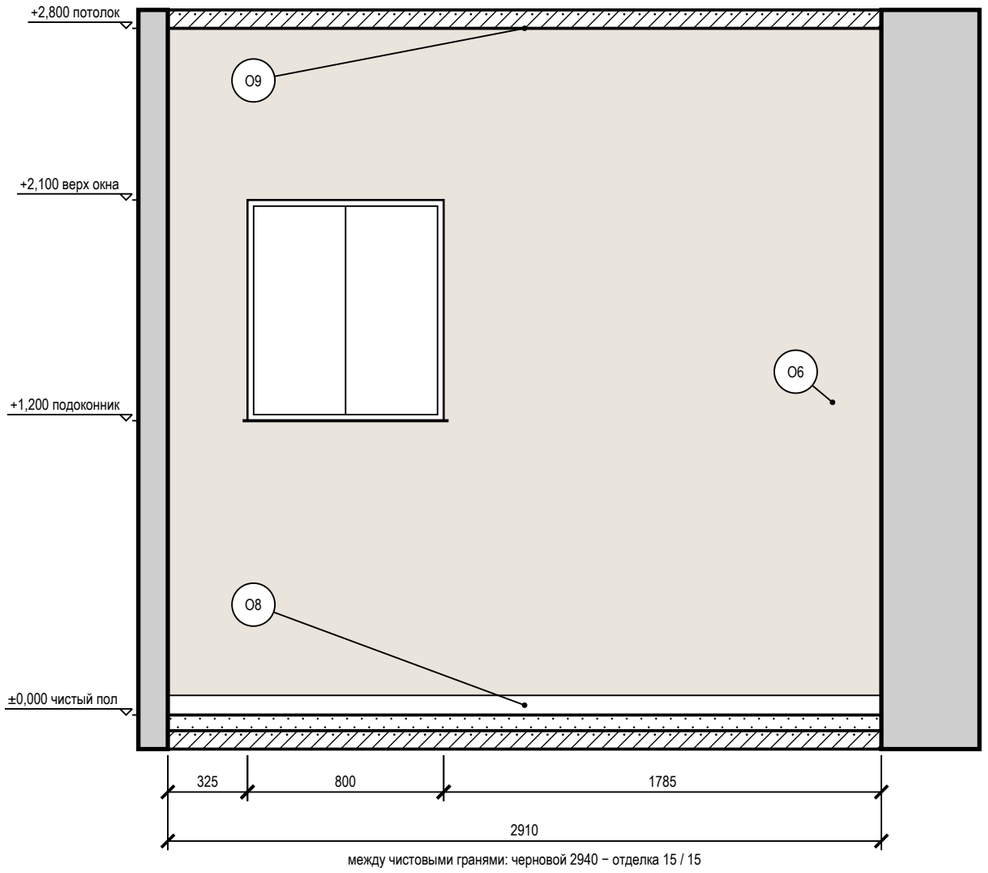


между чистовыми гранями: черновой 2940 − отделка 15 / 15

Развёртка стены Б

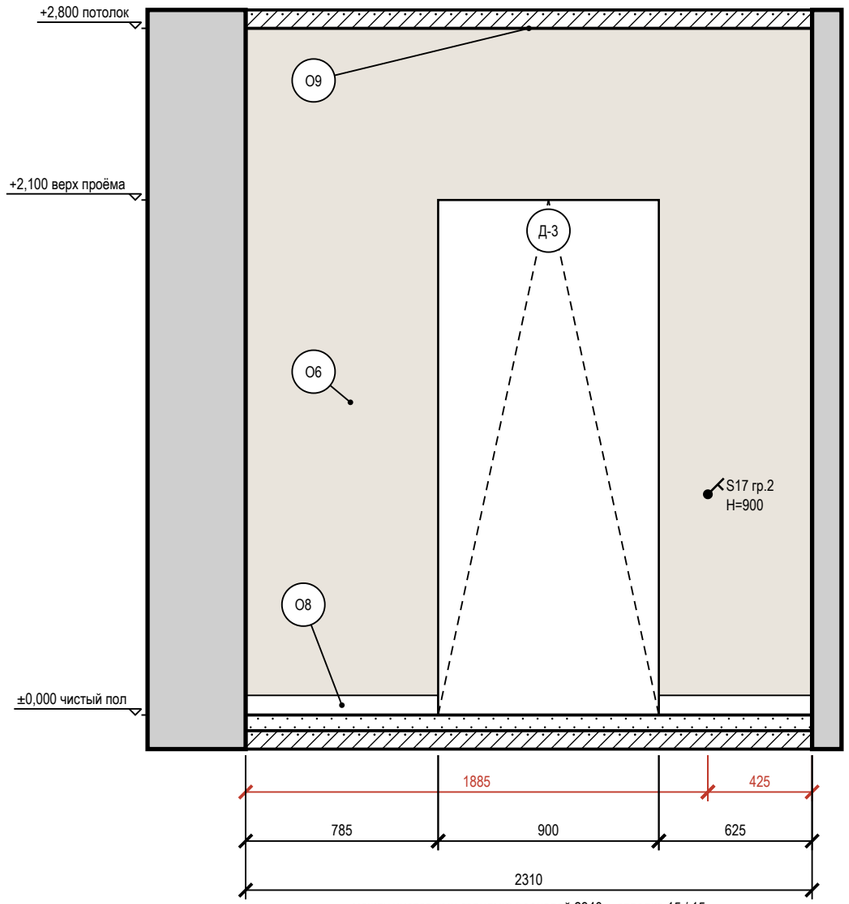

между чистовыми гранями: черновой 2340 − отделка 15 / 15

Схема развёрток (М 1:100)

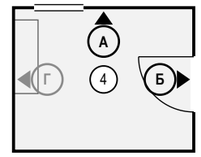

Допущения и предложения на листе

Основа листа: размеры и контуры этажей подобраны проектировщиком по составу помещений и площадям этажей с картинки 470 px (размеры на ней не читаются); обмер и исходный проект — задание (К-1); высоты: 1-й этаж 2800 мм, мансарда 2700 мм (горизонтальная часть) приняты; скаты кровли мансарды приняты по картинке: колено 1200 мм, уклон 45°, конёк вдоль длинной стороны; проект КР — задание (К-2); наружные стены 400 мм, перегородки 120 мм приняты (К-1); разрешённая мощность 15 кВт принята по типовым ТУ для частного дома (К-4); подрайон климата не задан — принят не северный (жилые от 2,5 м) (К-7).

См. лист открытых вопросов (лист 8, записи К-1, К-2, К-4, К-7).

Условные обозначения

- выключатель одноклавишный
- привязки точек и выводов от угла и от пола, мм
- мебель и приборы — фасад по расстановке (условно)
- окно: проём, рама, подоконник
- дверной проём; марка двери — в кружке
- стены и перекрытия в сечении
- окраска: тон — цвет по коду производителя (условно)
- О1 — марка отделки по реестру отделки альбома
- А — марка развёртки: буква стены, стрелка — взгляд

Ведомость отделки (на листе)

Марка	Поверхность	Материал, изделие	Цвет, код	Кол.
О6	стены	окраска, Farrow & Ball Modern Emulsion, матовая, подготовка Q3	Farrow & Ball No. 226 «Joa's White»	12 м²
О8	плинтус	плинтус МДФ, h 80 мм, аналог: плинтус МДФ под покраску 80×16	Farrow & Ball No. 226 «Joa's White»	4,3 м
О9	потолок	окраска, Little Greene Absolute Matt, глубокоматовая, подготовка Q3	Little Greene No. 105 «Slaked Lime»	6,9 м²

Примечания

1. Развёртки — вид на стену изнутри помещения, по часовой стрелке; расположение — на схеме листа и на листе 127; размеры — в мм по чистовым поверхностям; отметки — в м от ±0,000 (чистый пол 1-го этажа); высоты H — от чистого пола помещения до оси изделия, у декора — до центра.
2. Красная цепочка — привязки электроточек и выводов по осям от угла чистовых стен; высота H — у знака, от чистого пола до оси; высоты мебели, проёмов и границ отделки — колонкой отметок слева. Стена с 5 и более точками или с мелкими звеньями привязок показана двумя видами: архитектурная развёртка (мебель, отделка, проёмы, высоты) и вид «Привязки» на отдельном листе — точки и выводы с марками, одна цепочка по осям и таблица привязок (каждая точка — строка).
3. У знака электроточки: марка (Р — розетка, S — выключатель, Св — светильник, ЭВ — вывод кабеля), ×N — число постов в рамке, гр. — группа щита, H — высота оси от чистого пола, мм; группы по клавишам выключателя — на листе выключателей.
4. Схема мебели, приборов и декора не является технической документацией для производства мебели; габариты — по паспортам изделий.

1000 мм · печать 1:1

Изм.	Кол.уч	Лист	№ док.	Подп.	Дата
Разраб.		Кырлан А.С.			04.11.26
Пров.					
ГИП					
Н. контр.					
Утв.					

ГД-2026-010-АИ

Дом 331 м²

Общая площадь 270,67* м² · * размеры приняты, не замерены (реестр — л. 8–10, К-1)

Дизайн-проект интерьера

Стадия	Лист	Листов
РП	143	216

Развёртки стен А, Б. Котельная (пом. 4)

М 1:25


Кырлан Александр Сергеевич

выпуск 04.11.2026 № 2a77323a49 · стр. 147 из 221

Развёртка стены Г. Котельная (пом. 4)


Котельная (пом. 4) · вид изнутри помещения · размеры в мм, отметки в м от ±0,000 (чистый пол 1-го этажа)

Развёртка стены Г

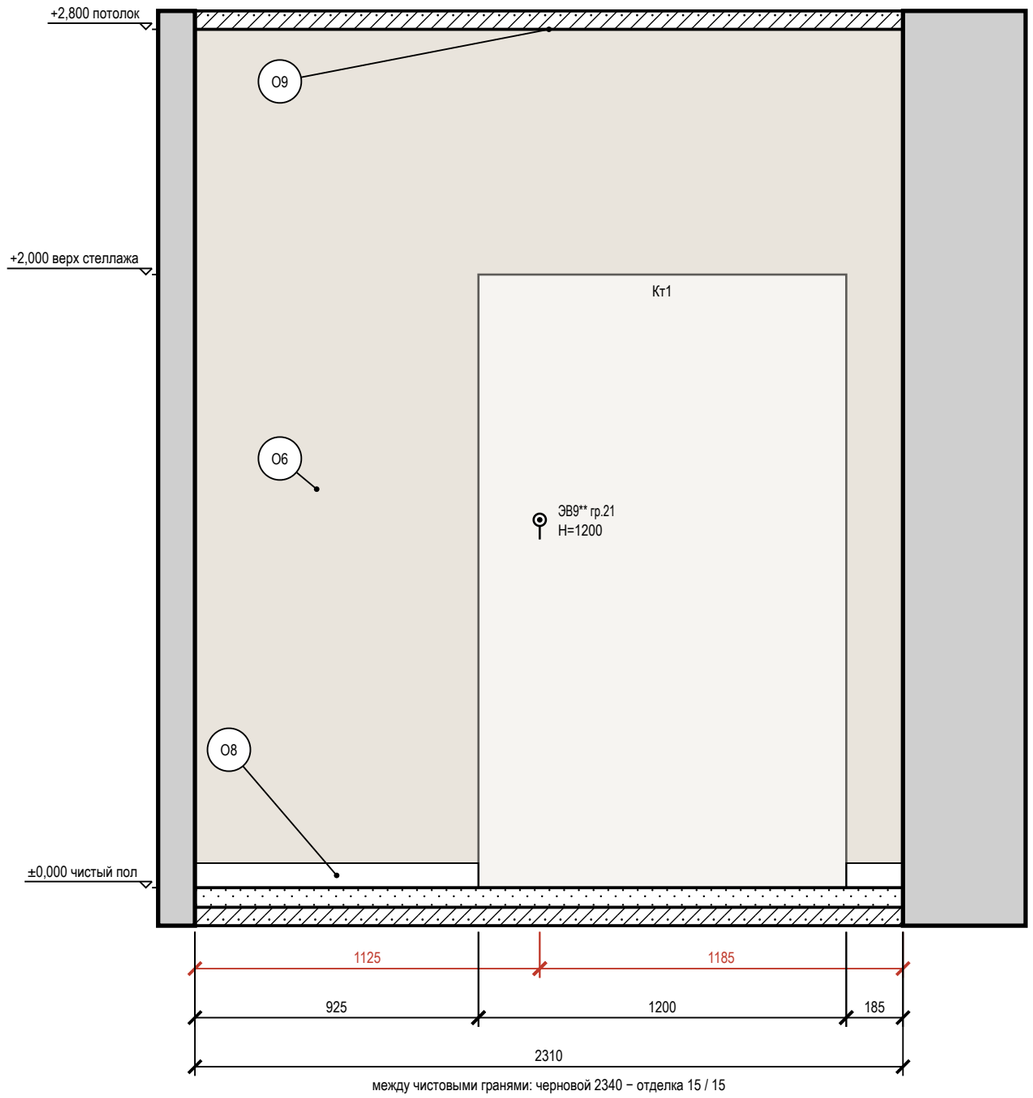

между чистовыми гранями: черновой 2340 − отделка 15 / 15

Схема развёрток (М 1:100)

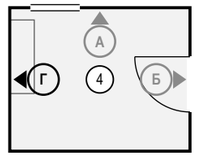

Условные обозначения

- вывод кабеля для подключения прибора (без розетки), марка ЭВ
- привязки точек и выводов от угла и от пола, мм
- мебель и приборы — фасад по расстановке (условно)
- стены и перекрытия в сечении
- окраска: тон — цвет по коду производителя (условно)
- О1 — марка отделки по реестру отделки альбома
- А — марка развёртки: буква стены, стрелка — взгляд

Ведомость отделки (на листе)

Марка	Поверхность	Материал, изделие	Цвет, код	Кол.
О6	стены	окраска, Farrow & Ball Modern Emulsion, матовая, подготовка Q3	Farrow & Ball No. 226 «Joa's White»	6,5 м²
О8	плинтус	плинтус МДФ, h 80 мм, аналог: плинтус МДФ под покраску 80×16	Farrow & Ball No. 226 «Joa's White»	1,1 м
О9	потолок	окраска, Little Greene Absolute Matt, глубокоматовая, подготовка Q3	Little Greene No. 105 «Slaked Lime»	6,9 м²

Допущения и предложения на листе

Основа листа: размеры и контуры этажей подобраны проектировщиком по составу помещений и площадям этажей с картинки 470 px (размеры на ней не читаются); обмер и исходный проект — задание (К-1); высоты: 1-й этаж 2800 мм, мансарда 2700 мм (горизонтальная часть) приняты; скаты кровли мансарды приняты по картинке: колено 1200 мм, уклон 45°, конёк вдоль длинной стороны; проект КР — задание (К-2); наружные стены 400 мм, перегородки 120 мм приняты (К-1); разрешённая мощность 15 кВт принята по типовым ТУ для частного дома (К-4); подрайон климата не задан — принят не северный (жилые от 2,5 м) (К-7).

Знак «**» — предложение проектировщика, заказчиком не утверждено (согласовать с заказчиком): ЭВ9 — место и тип котла не выбраны (газ / электро — вопрос заказчику): вывод у стены D, уточнить по проекту котельной.

См. лист открытых вопросов (лист 8, записи К-1, К-2, К-4, К-7).

Примечания

1. Развёртки — вид на стену изнутри помещения, по часовой стрелке; расположение — на схеме листа и на листе 127; размеры — в мм по чистовым поверхностям; отметки — в м от ±0,000 (чистый пол 1-го этажа); высоты H — от чистого пола помещения до оси изделия, у декора — до центра.
2. Красная цепочка — привязки электроточек и выводов по осям от угла чистовых стен; высота H — у знака, от чистого пола до оси; высоты мебели, проёмов и границ отделки — колонкой отметок слева. Стена с 5 и более точками или с мелкими звеньями привязок показана двумя видами: архитектурная развёртка (мебель, отделка, проёмы, высоты) и вид «Привязки» на отдельном листе — точки и выводы с марками, одна цепочка по осям и таблица привязок (каждая точка — строка).
3. У знака электроточки: марка (Р — розетка, S — выключатель, Св — светильник, ЭВ — вывод кабеля), ×N — число постов в рамке, гр. — группа щита, H — высота оси от чистого пола, мм; группы по клавишам выключателя — на листе выключателей.
4. Схема мебели, приборов и декора не является технической документацией для производства мебели; габариты — по паспортам изделий.

1000 мм · печать 1:1

Изм.	Кол.уч	Лист	№ док.	Подп.	Дата
Разраб.		Кырлан А.С.			04.11.26
Пров.					
ГИП					
Н. контр.					
Утв.					

ГД-2026-010-АИ

Дом 331 м²

Общая площадь 270,67* м² · * размеры приняты, не замерены (реестр — л. 8–10, К-1)

Дизайн-проект интерьера

Стадия	Лист	Листов
РП	144	216

Развёртка стены Г. Котельная (пом. 4)

М 1:20

Кырлан Александр Сергеевич


выпуск 04.11.2026 № 2a77323a49 · стр. 148 из 221

Развёртка стены А. Гостиная (пом. 5)

Гостиная (пом. 5) · вид изнутри помещения · размеры в мм, отметки в м от ±0,000 (чистый пол 1-го этажа)


ПРЕДВАРИТЕЛЬНО · не для производства работ · открыто пунктов: 15 (реестр — л. 8–10)

Развёртка стены А

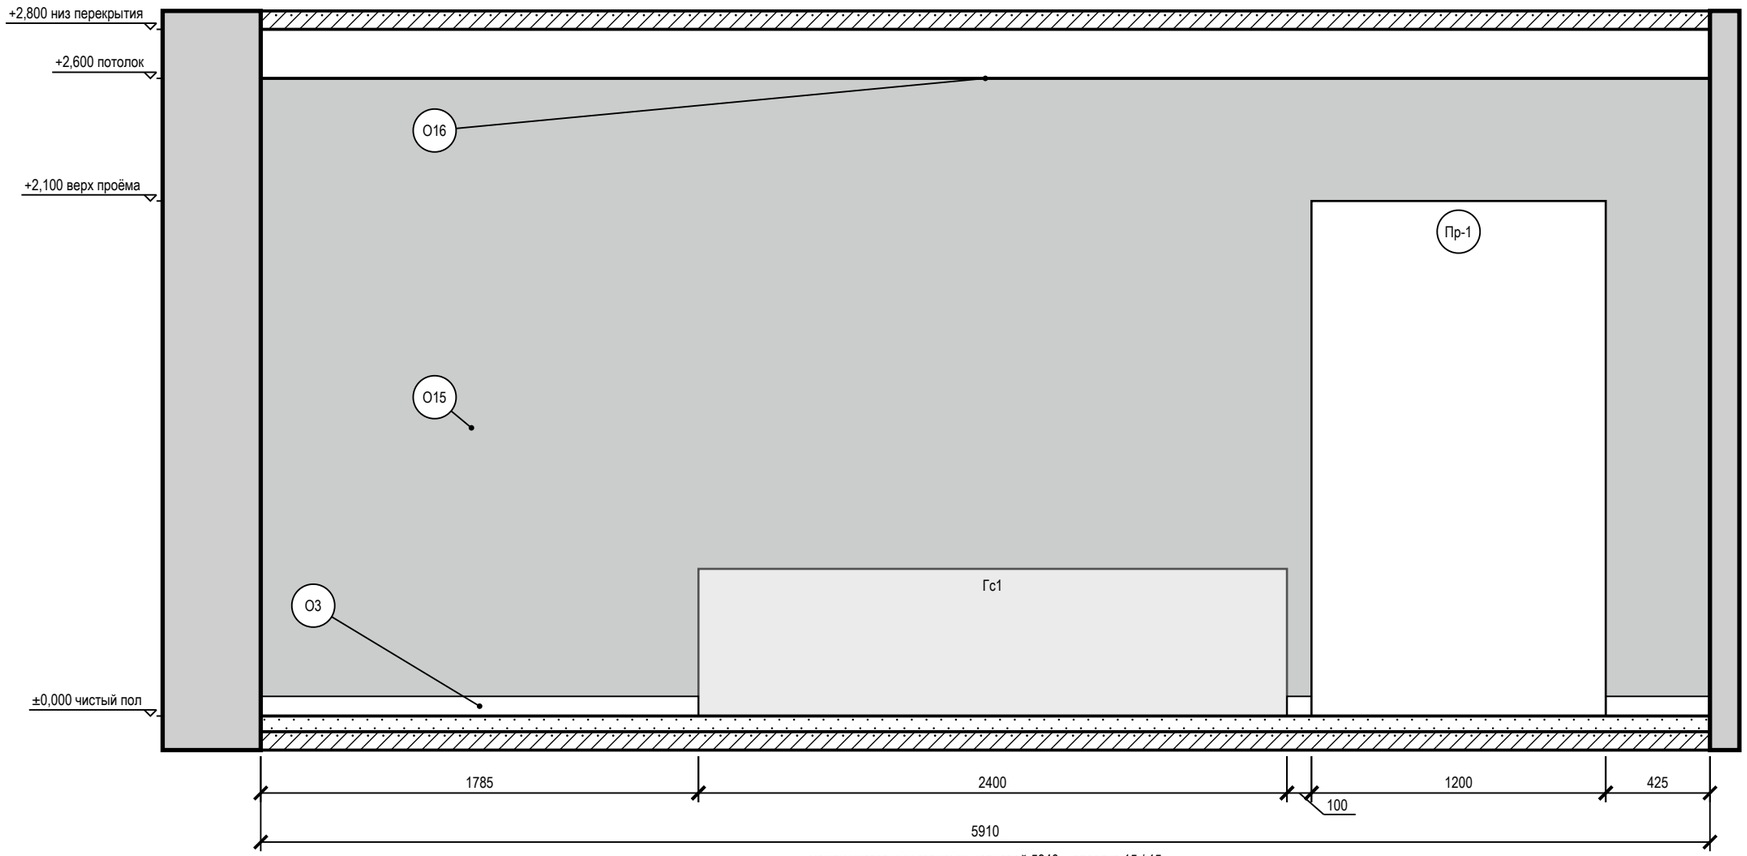

между чистовыми гранями: черновой 5940 − отделка 15 / 15

Схема развёрток (М 1:100)

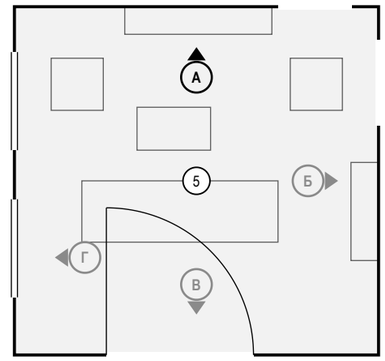

Условные обозначения

- мебель и приборы — фасад по расстановке (условно)
- дверной проём; марка двери — в кружке
- стены и перекрытия в сечении
- окраска: тон — цвет по коду производителя (условно)
- О1 — марка отделки по реестру отделки альбома
- А — марка развёртки: буква стены, стрелка — взгляд

Ведомость отделки (на листе)

Марка	Поверхность	Материал, изделие	Цвет, код	Кол.
О3	плинтус	плинтус МДФ, h 80 мм, аналог: плинтус МДФ под окраску 80×16 мм, полуглянцевая	NCS S 0804-Y30R «S 0804-Y30R»	2,3 м
О15	акцентная стена	окраска, Farrow & Ball Modern Emulsion, аналог: интерьерная краска, класс 2 по EN 13300, глубокоматовая/матовая, база C, матовая, подготовка К3	Farrow & Ball No. 93 «Studio Green — почти чёрный зелёный»	12,8 м²
О16	потолок	окраска, Tikkurila Anti-Reflex 2, глубокоматовая, подготовка Q3	NCS S 0804-Y30R «S 0804-Y30R»	33,7 м²

Допущения и предложения на листе

Основа листа: размеры и контуры этажей подобраны проектировщиком по составу помещений и площадям этажей с картинки 470 px (размеры на ней не читаются); обмер и исходный проект — задание (К-1); высоты: 1-й этаж 2800 мм, мансарда 2700 мм (горизонтальная часть) приняты; скаты кровли мансарды приняты по картинке: колено 1200 мм, уклон 45°, конёк вдоль длинной стороны; проект КР — задание (К-2); наружные стены 400 мм, перегородки 120 мм приняты (К-1); разрешённая мощность 15 кВт принята по типовым ТУ для частного дома (К-4); подрайон климата не задан — принят не северный (жилые от 2,5 м) (К-7).

Знак «**» — предложение проектировщика, заказчиком не утверждено (согласовать с заказчиком): К-9: дверь пом. 5 (стена В) — проём 2400×2100 на веранду с картинки: одной распашной створкой не закрывается (полотна 600–900) — раздвижная двустворчатая, остеклённая; система и полотна — по каталогу после утверждения автором.

См. лист открытых вопросов (лист 8, записи К-1, К-2, К-4, К-7; лист 9, запись К-9).

Примечания

1. Развёртки — вид на стену изнутри помещения, по часовой стрелке; расположение — на схеме листа и на листе 127; размеры — в мм по чистовым поверхностям; отметки — в м от ±0,000 (чистый пол 1-го этажа); высоты Н — от чистого пола помещения до оси изделия, у декора — до центра.
2. Стена А показана двумя видами: здесь — архитектурная развёртка (мебель, отделка, проёмы, высоты), электроточки и выводы ВК с привязками и таблицей — на листе 146 («Привязки»).
3. Схема мебели, приборов и декора не является технической документацией для производства мебели; габариты — по паспортам изделий.
4. Потолок — у каждой стены свой, по плану потолков (ПТ2); ступени — зоной, кромка короба перед нишей — тонкой линией; в поле потолка: ПТ3 +2,700.

1000 мм · печать 1:1

Изм.	Кол.уч	Лист	№ док.	Подп.	Дата
Разраб.		Кырлан А.С.			04.11.26
Пров.					
ГИП					
Н. контр.					
Утв.					

ГД-2026-010-АИ

Дом 331 м²

Общая площадь 270,67* м² · * размеры приняты, не замерены (реестр — л. 8–10, К-1)

Дизайн-проект интерьера

Стадия	Лист	Листов
РП	145	216

Развёртка стены А. Гостиная (пом. 5)

М 1:25

Кырлан Александр Сергеевич

выпуск 04.11.2026 № 2a77323a49 · стр. 149 из 221

Привязки электроточек, стена А. Гостиная (пом. 5)

Гостиная (пом. 5) · вид изнутри помещения · привязки в мм, отметки в м · к развёртке на листе 145

Развёртка стены А: электроточки и выводы

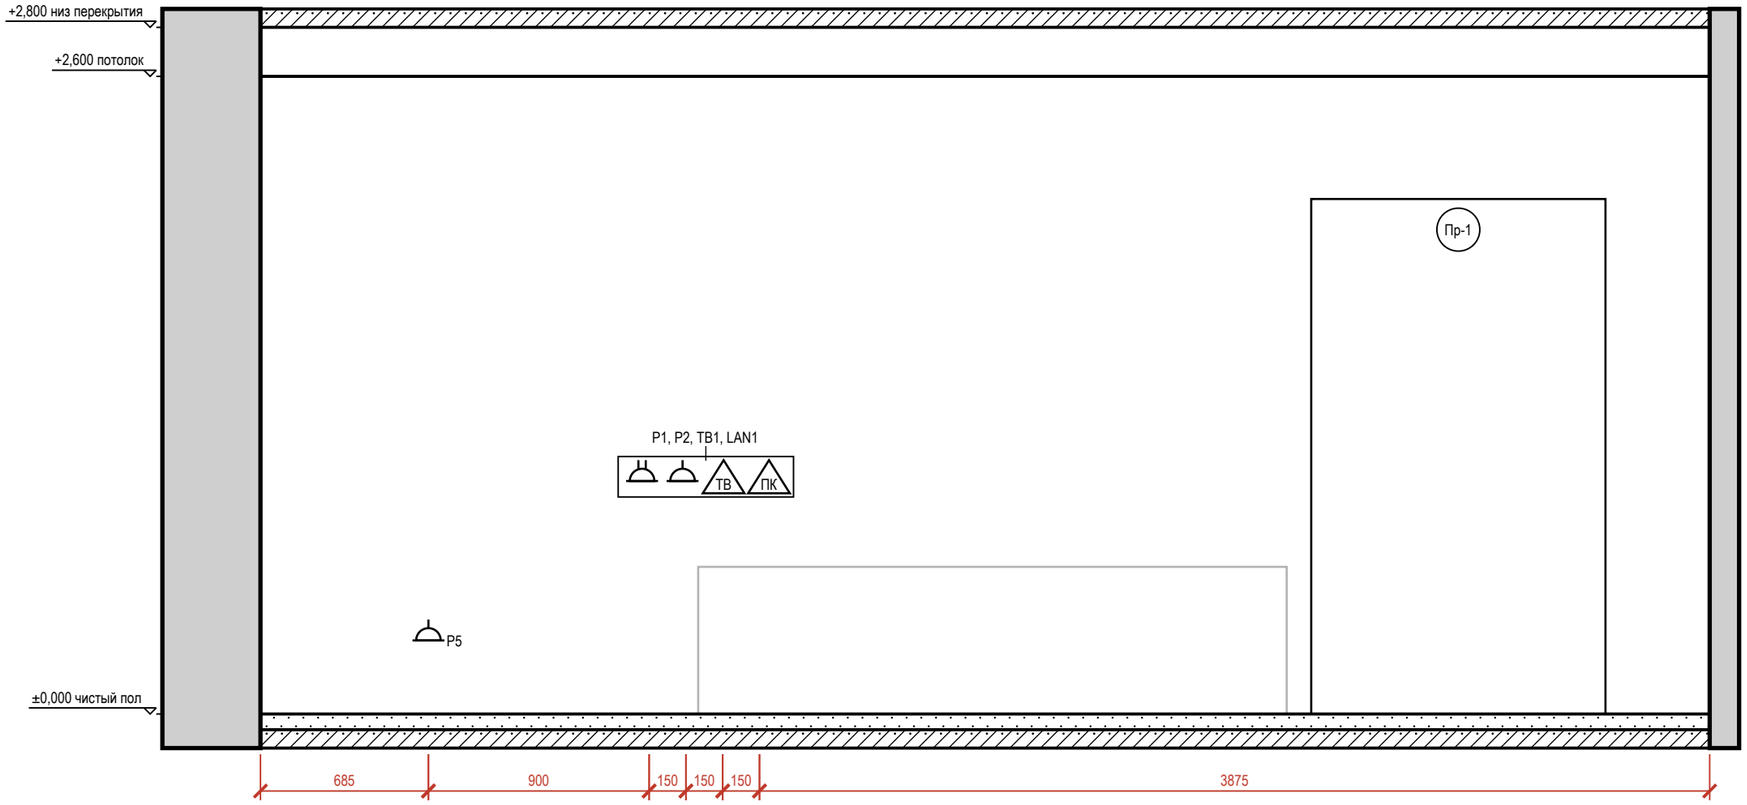


Таблица привязок электроточек и выводов

Марка	Назначение	От угла, мм	Н от пола, мм	Примечание
P5	розетка: общего назначения	685	300	гр. 5
P1	розетка: ТВ-зона: телевизор, медиаплеер	1585	950	рамка 2 поста, гр. 5
P2	розетка: ТВ-зона: саундбар	1735	950	гр. 5
TB1	розетка ТВ: ТВ-зона	1885	950	
LAN1	розетка RJ45: ТВ-зона	2035	950	

Условные обозначения

- розетка с заземляющим контактом; у знака — марка, ×N постов в рамке, гр. — группа щита, Н — высота оси, мм
- ПК — розетка компьютерная RJ45
- ТВ — розетка телевизионная
- привязки точек и выводов от угла и от пола, мм

Примечания

1. Вид «Привязки» стены А — электроточки и выводы ВК; архитектурная развёртка (мебель, отделка, проёмы, высоты) — на листе 145, расположение — на листе 127. Мебель и приборы — подложкой для ориентира; их марки и обозначения мебели, проёмов и стен — там же.
2. Привязки — в мм: по горизонтали от левого чистового угла стены до оси изделия, Н — от чистого пола до оси; все точки — в таблице привязок. Красная цепочка — привязки по осям; точки ближе 150 мм одна к другой в цепочку не дробятся — их привязки только в таблице.
3. У знака — марка электроточки (Р — розетка, S — выключатель, Св — светильник, ЭВ — вывод кабеля); посты в рамке и группа щита — в графе «Примечание»; группы по клавишам выключателя — на листе выключателей.

Допущения и предложения на листе

Основа листа: размеры и контуры этажей подобраны проектировщиком по составу помещений и площадям этажей с картинки 470 px (размеры на ней не читаются); обмер и исходный проект — задание (К-1); высоты: 1-й этаж 2800 мм, мансарда 2700 мм (горизонтальная часть) приняты; скаты кровли мансарды приняты по картинке: колено 1200 мм, уклон 45°, конёк вдоль длинной стороны; проект КР — задание (К-2); наружные стены 400 мм, перегородки 120 мм приняты (К-1); разрешённая мощность 15 кВт принята по типовым ТУ для частного дома (К-4); подрайон климата не задан — принят не северный (жилые от 2,5 м) (К-7).

Знак «**» — предложение проектировщика, заказчиком не утверждено (согласовать с заказчиком): К-9: дверь пом. 5 (стена В) — проём 2400×2100 на веранду с картинки: одной распашной створкой не закрывается (полотна 600–900) — раздвижная двустворчатая, остеклённая; система и полотна — по каталогу после утверждения автором.

См. лист открытых вопросов (лист 8, записи К-1, К-2, К-4, К-7; лист 9, запись К-9).

1000 мм · печать 1:1

Изм.	Кол.уч	Лист	№ док.	Подп.	Дата
Разраб.		Кырлан А.С.			04.11.26
Пров.					
ГИП					
Н. контр.					
Утв.					

ГД-2026-010-АИ

Дом 331 м²

Общая площадь 270,67* м² · * размеры приняты, не замерены (реестр — л. 8–10, К-1)

Дизайн-проект интерьера

Стадия	Лист	Листов
РП	146	216

Привязки электроточек, стена А. Гостиная (пом. 5)

М 1:25

Кырлан Александр Сергеевич


выпуск 04.11.2026 № 2a77323a49 · стр. 150 из 221

Развёртка стены Б. Гостиная (пом. 5)

Гостиная (пом. 5) · вид изнутри помещения · размеры в мм, отметки в м от ±0,000 (чистый пол 1-го этажа)


ПРЕДВАРИТЕЛЬНО · не для производства работ · открыто пунктов: 15 (реестр — л. 8–10)

Развёртка стены Б

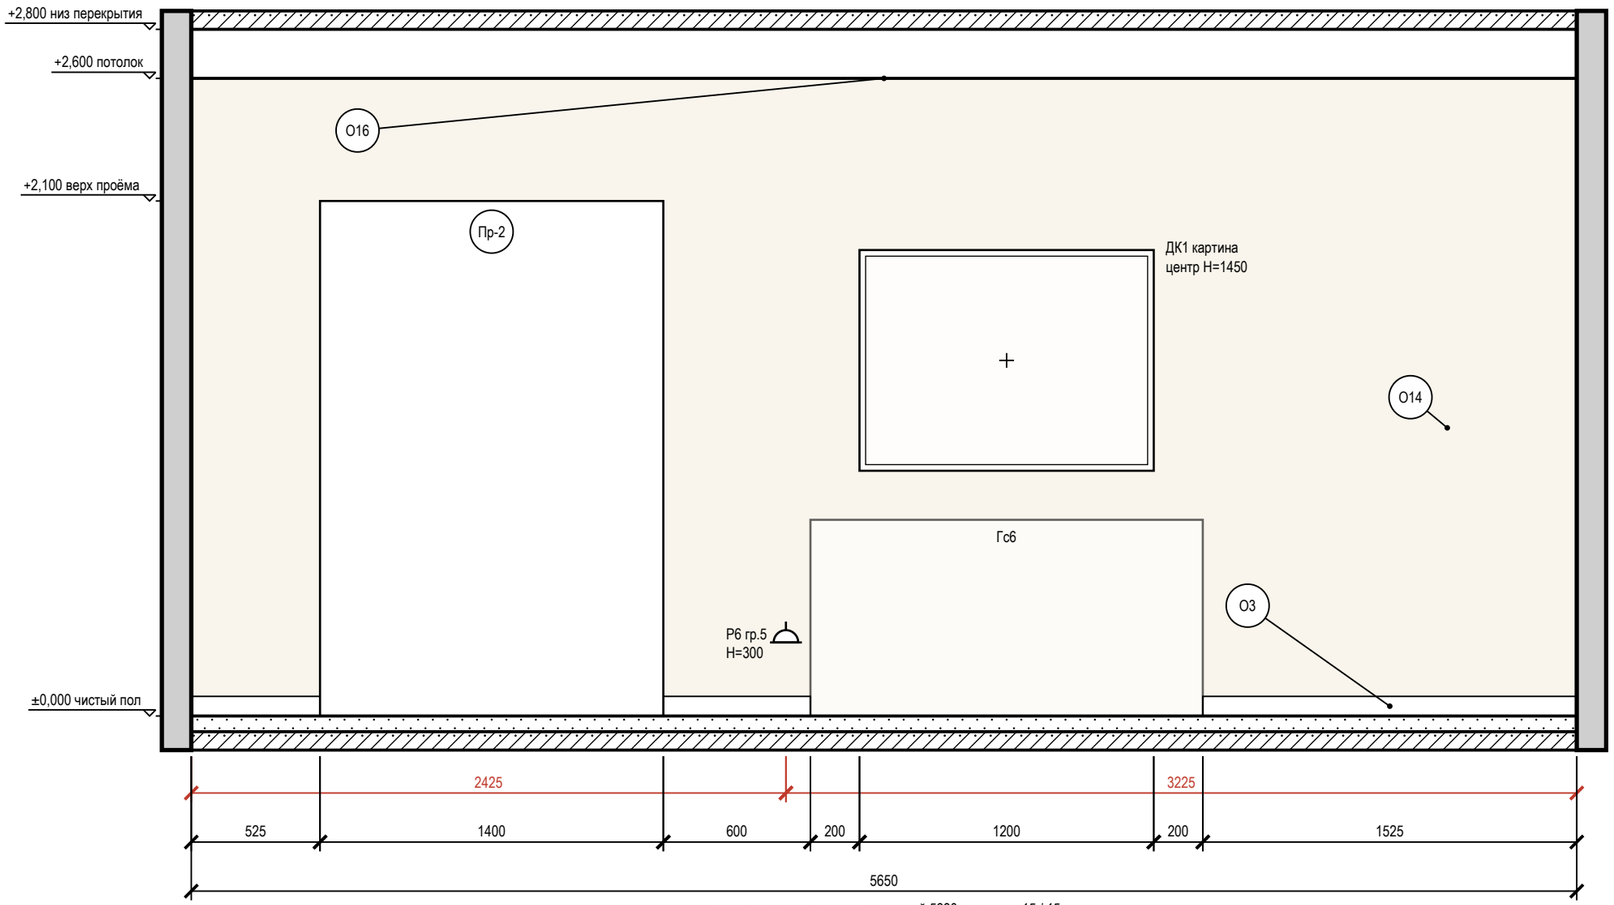

между чистовыми гранями: черновой 5680 − отделка 15 / 15

Схема развёрток (М 1:100)

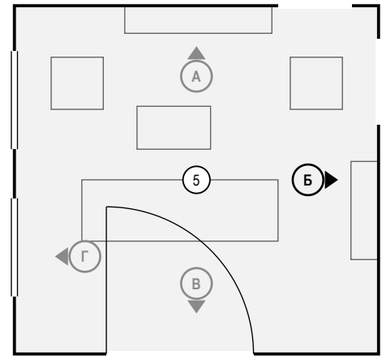

Условные обозначения

- розетка с заземляющим контактом; у знака — марка, ×N постов в рамке, гр. — группа щита, Н — высота оси, мм
- привязки точек и выводов от угла и от пола, мм
- мебель и приборы — фасад по расстановке (условно)
- картина (декор): марка Д, крест — центр, Н — высота центра, мм
- дверной проём; марка двери — в кружке
- стены и перекрытия в сечении
- окраска: тон — цвет по коду производителя (условно)
- О1 — марка отделки по реестру отделки альбома
- А — марка развёртки: буква стены, стрелка — взгляд

Ведомость отделки (на листе)

Марка	Поверхность	Материал, изделие	Цвет, код	Кол.
О3	плинтус	плинтус МДФ, h 80 мм, аналог: плинтус МДФ под окраску 80×16 мм, полуглянцевая	NCS S 0804-Y30R «S 0804-Y30R»	2,6 м
О14	стены	окраска, Tikkurila Optiva 5 Matt, матовая, подготовка К3	NCS S 0804-Y30R «S 0804-Y30R»	11,8 м²
О16	потолок	окраска, Tikkurila Anti-Reflex 2, глубокоматовая, подготовка Q3	NCS S 0804-Y30R «S 0804-Y30R»	33,7 м²

Примечания

1. Развёртки — вид на стену изнутри помещения, по часовой стрелке; расположение — на схеме листа и на листе 127; размеры — в мм по чистовым поверхностям; отметки — в м от ±0,000 (чистый пол 1-го этажа); высоты Н — от чистого пола помещения до оси изделия, у декора — до центра.
2. Красная цепочка — привязки электроточек и выводов по осям от угла чистовых стен; высота Н — у знака, от чистого пола до оси; высоты мебели, проёмов и границ отделки — колонкой отметок слева. Стена с 5 и более точками или с мелкими звеньями привязок показана двумя видами: архитектурная развёртка (мебель, отделка, проёмы, высоты) и вид «Привязки» на отдельном листе — точки и выводы с марками, одна цепочка по осям и таблица привязок (каждая точка — строка).
3. У знака электроточки: марка (Р — розетка, S — выключатель, Св — светильник, ЭВ — вывод кабеля), ×N — число постов в рамке, гр. — группа щита, Н — высота оси от чистого пола, мм; группы по клавишам выключателя — на листе выключателей.
4. Схема мебели, приборов и декора не является технической документацией для производства мебели; габариты — по паспортам изделий.
5. Картины и зеркала крепить к основанию по паспорту изделия (закладные и анкеры — в перечне скрытых работ); крест — ось центра предмета.
6. Потолок — у каждой стены свой, по плану потолков (ПТ2); ступени — зоной, кромка короба перед нишей — тонкой линией; в поле потолка: ПТ3 +2,700.

1000 мм · печать 1:1

Допущения и предложения на листе

Основа листа: размеры и контуры этажей подобраны проектировщиком по составу помещений и площадям этажей с картинки 470 px (размеры на ней не читаются); обмер и исходный проект — задание (К-1); высоты: 1-й этаж 2800 мм, мансарда 2700 мм (горизонтальная часть) приняты; скаты кровли мансарды приняты по картинке: колено 1200 мм, уклон 45°, конёк вдоль длинной стороны; проект КР — задание (К-2); наружные стены 400 мм, перегородки 120 мм приняты (К-1); разрешённая мощность 15 кВт принята по типовым ТУ для частного дома (К-4); подрайон климата не задан — принят не северный (жилые от 2,5 м) (К-7).

Знак «**» — предложение проектировщика, заказчиком не утверждено (согласовать с заказчиком): К-9: дверь пом. 5 (стена В) — проём 2400×2100 на веранду с картинки: одной распашной створкой не закрывается (полотна 600–900) — раздвижная двустворчатая, остеклённая; система и полотна — по каталогу после утверждения автором.

См. лист открытых вопросов (лист 8, записи К-1, К-2, К-4, К-7; лист 9, запись К-9).

Изм.	Кол.уч	Лист	№ док.	Подп.	Дата	ГД-2026-010-АИ			
						Дом 331 м²			
						Общая площадь 270,67* м² · * размеры приняты, не замерены (реестр — л. 8–10, К-1)			
Разраб.		Кырлан А.С.			04.11.26	Дизайн-проект интерьера	Стадия	Лист	Листов
Пров.							РП	147	216
ГИП									
						Развёртка стены Б. Гостиная (пом. 5)	Кырлан Александр Сергеевич		
Н. контр.									
Утв.						М 1:25			


выпуск 04.11.2026 № 2a77323a49 · стр. 151 из 221

Развёртка стены В. Гостиная (пом. 5)

Гостиная (пом. 5) · вид изнутри помещения · размеры в мм, отметки в м от ±0,000 (чистый пол 1-го этажа)


ПРЕДВАРИТЕЛЬНО · не для производства работ · открыто пунктов: 15 (реестр — л. 8–10)

Развёртка стены В

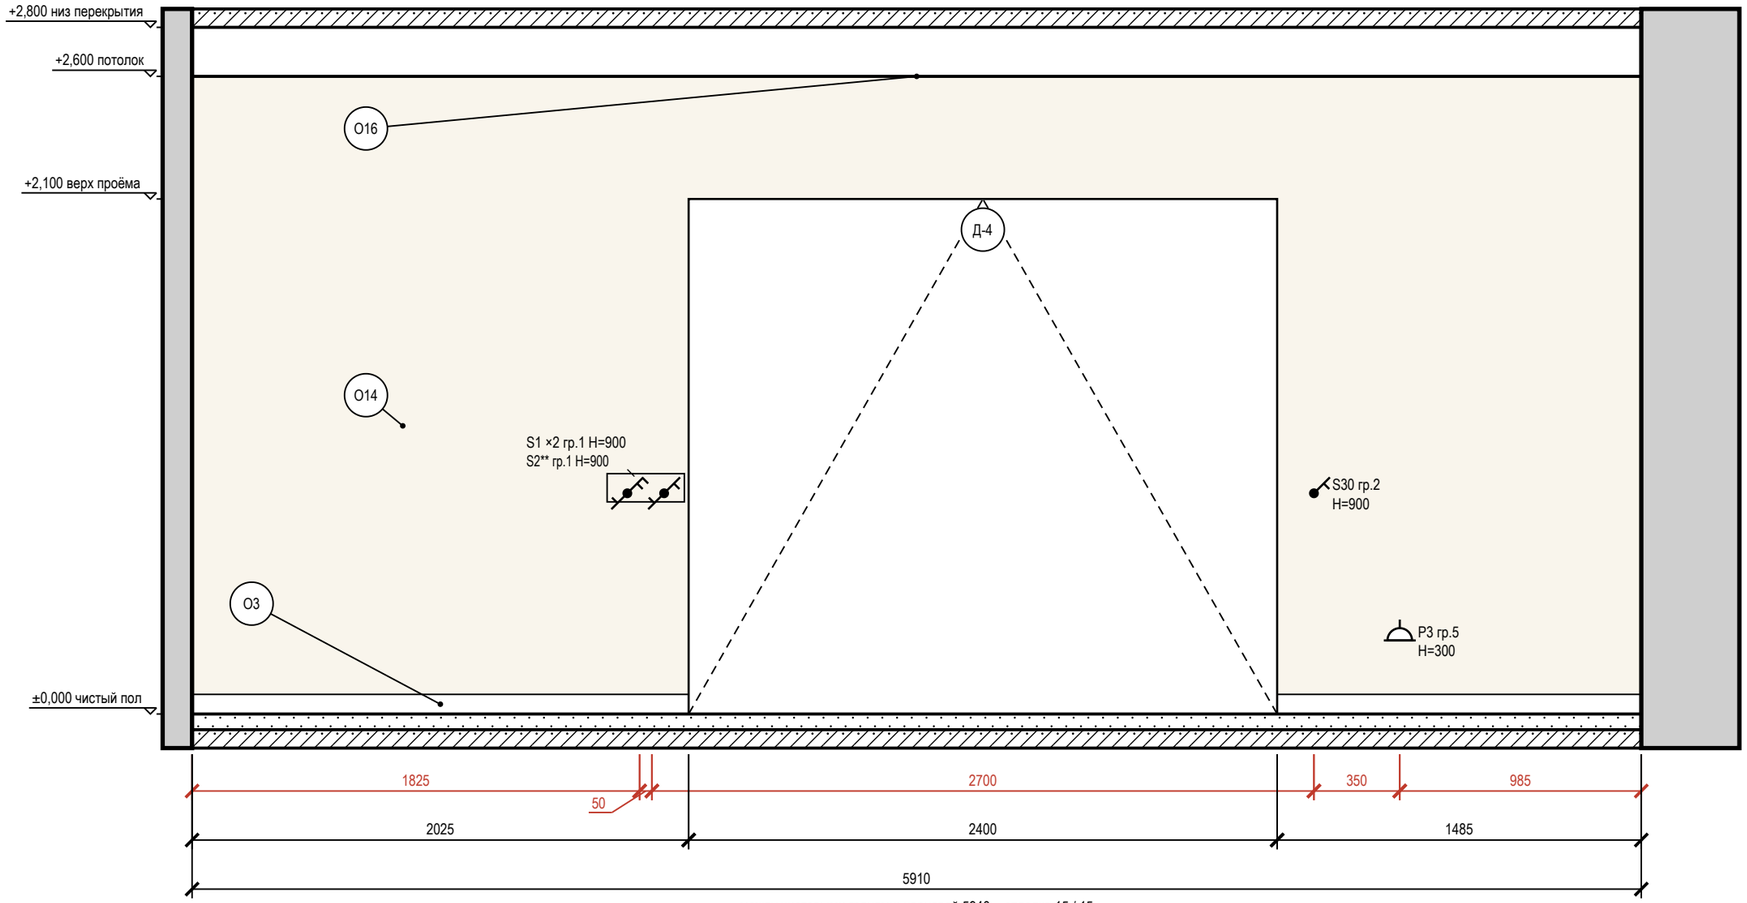

между чистовыми гранями: черновой 5940 − отделка 15 / 15

Схема развёрток (М 1:100)

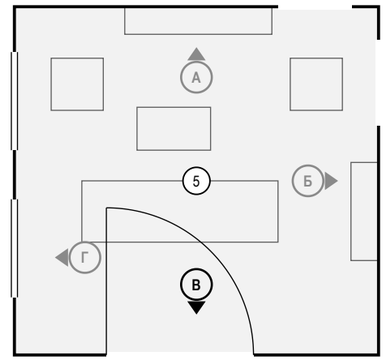

Условные обозначения

- розетка с заземляющим контактом; у знака — марка, ×N постов в рамке, гр. — группа щита, H — высота оси, мм
- выключатель одноклавишный
- выключатель двухклавишный (флажков — по числу клавиш)
- выключатель с проходной или перекрёстной клавишей (обратный флажок); тип клавиши — в подписи
- привязки точек и выводов от угла и от пола, мм
- мебель и приборы — фасад по расстановке (условно)
- дверной проём; марка двери — в кружке
- стены и перекрытия в сечении
- окраска: тон — цвет по коду производителя (условно)
- О1 — марка отделки по реестру отделки альбома
- А — марка развёртки: буква стены, стрелка — взгляд

Ведомость отделки (на листе)

Марка	Поверхность	Материал, изделие	Цвет, код	Кол.
О3	плинтус	плинтус МДФ, h 80 мм, аналог: плинтус МДФ под окраску 80×16 мм, полуглянцевая	NCS S 0804-Y30R «S 0804-Y30R»	3,5 м
О14	стены	окраска, Tikkurila Optiva 5 Matt, матовая, подготовка К3	NCS S 0804-Y30R «S 0804-Y30R»	10,3 м²
О16	потолок	окраска, Tikkurila Anti-Reflex 2, глубокоматовая, подготовка Q3	NCS S 0804-Y30R «S 0804-Y30R»	33,7 м²

Примечания

1. Развёртки — вид на стену изнутри помещения, по часовой стрелке; расположение — на схеме листа и на листе 127; размеры — в мм по чистовым поверхностям; отметки — в м от ±0,000 (чистый пол 1-го этажа); высоты H — от чистого пола помещения до оси изделия, у декора — до центра.
2. Красная цепочка — привязки электроточек и выводов по осям от угла чистовых стен; высота H — у знака, от чистого пола до оси; высоты мебели, проёмов и границ отделки — колонкой отметок слева. Стена с 5 и более точками или с мелкими звеньями привязок показана двумя видами: архитектурная развёртка (мебель, отделка, проёмы, высоты) и вид «Привязки» на отдельном листе — точки и выводы с марками, одна цепочка по осям и таблица привязок (каждая точка — строка).
3. У знака электроточки: марка (Р — розетка, S — выключатель, Св — светильник, ЭВ — вывод кабеля), ×N — число постов в рамке, гр. — группа щита, H — высота оси от чистого пола, мм; группы по клавишам выключателя — на листе выключателей.
4. Схема мебели, приборов и декора не является технической документацией для производства мебели; габариты — по паспортам изделий.
5. Потолок — у каждой стены свой, по плану потолков (ПТ2); ступени — зоной, кромка короба перед нишей — тонкой линией; в поле потолка: ПТ3 +2,700.

1000 мм · печать 1:1

Допущения и предложения на листе

Основа листа: размеры и контуры этажей подобраны проектировщиком по составу помещений и площадям этажей с картинки 470 px (размеры на ней не читаются); обмер и исходный проект — задание (К-1); высоты: 1-й этаж 2800 мм, мансарда 2700 мм (горизонтальная часть) приняты; скаты кровли мансарды приняты по картинке: колено 1200 мм, уклон 45°, конёк вдоль длинной стороны; проект КР — задание (К-2); наружные стены 400 мм, перегородки 120 мм приняты (К-1); разрешённая мощность 15 кВт принята по типовым ТУ для частного дома (К-4); подрайон климата не задан — принят не северный (жилые от 2,5 м) (К-7).

Знак «**» — предложение проектировщика, заказчиком не утверждено (согласовать с заказчиком): S2 — светорегулятор добавлен под диммируемую ленту L3; уровни сценариев выбраны конвейером; К-9: дверь пом. 5 (стена В) — проём 2400×2100 на веранду с картинки: одной распашной створкой не закрывается (полотна 600–900) — раздвижная двустворчатая, остеклённая; система и полотна — по каталогу после утверждения автором.

См. лист открытых вопросов (лист 8, записи К-1, К-2, К-4, К-7; лист 9, запись К-9).

Изм.	Кол.уч	Лист	№ док.	Подп.	Дата
Разраб.		Кырлан А.С.			04.11.26
Пров.					
ГИП					
Н. контр.					
Утв.					

ГД-2026-010-АИ

Дом 331 м²

Общая площадь 270,67* м² · * размеры приняты, не замерены (реестр — л. 8–10, К-1)

Дизайн-проект интерьера

Стадия	Лист	Листов
РП	148	216

Развёртка стены В. Гостиная (пом. 5)

М 1:25

Кырлан Александр Сергеевич


выпуск 04.11.2026 № 2a77323a49 · стр. 152 из 221

Развёртка стены Г. Гостиная (пом. 5)

Гостиная (пом. 5) · вид изнутри помещения · размеры в мм, отметки в м от ±0,000 (чистый пол 1-го этажа)


ПРЕДВАРИТЕЛЬНО · не для производства работ · открыто пунктов: 15 (реестр — л. 8–10)

Развёртка стены Г

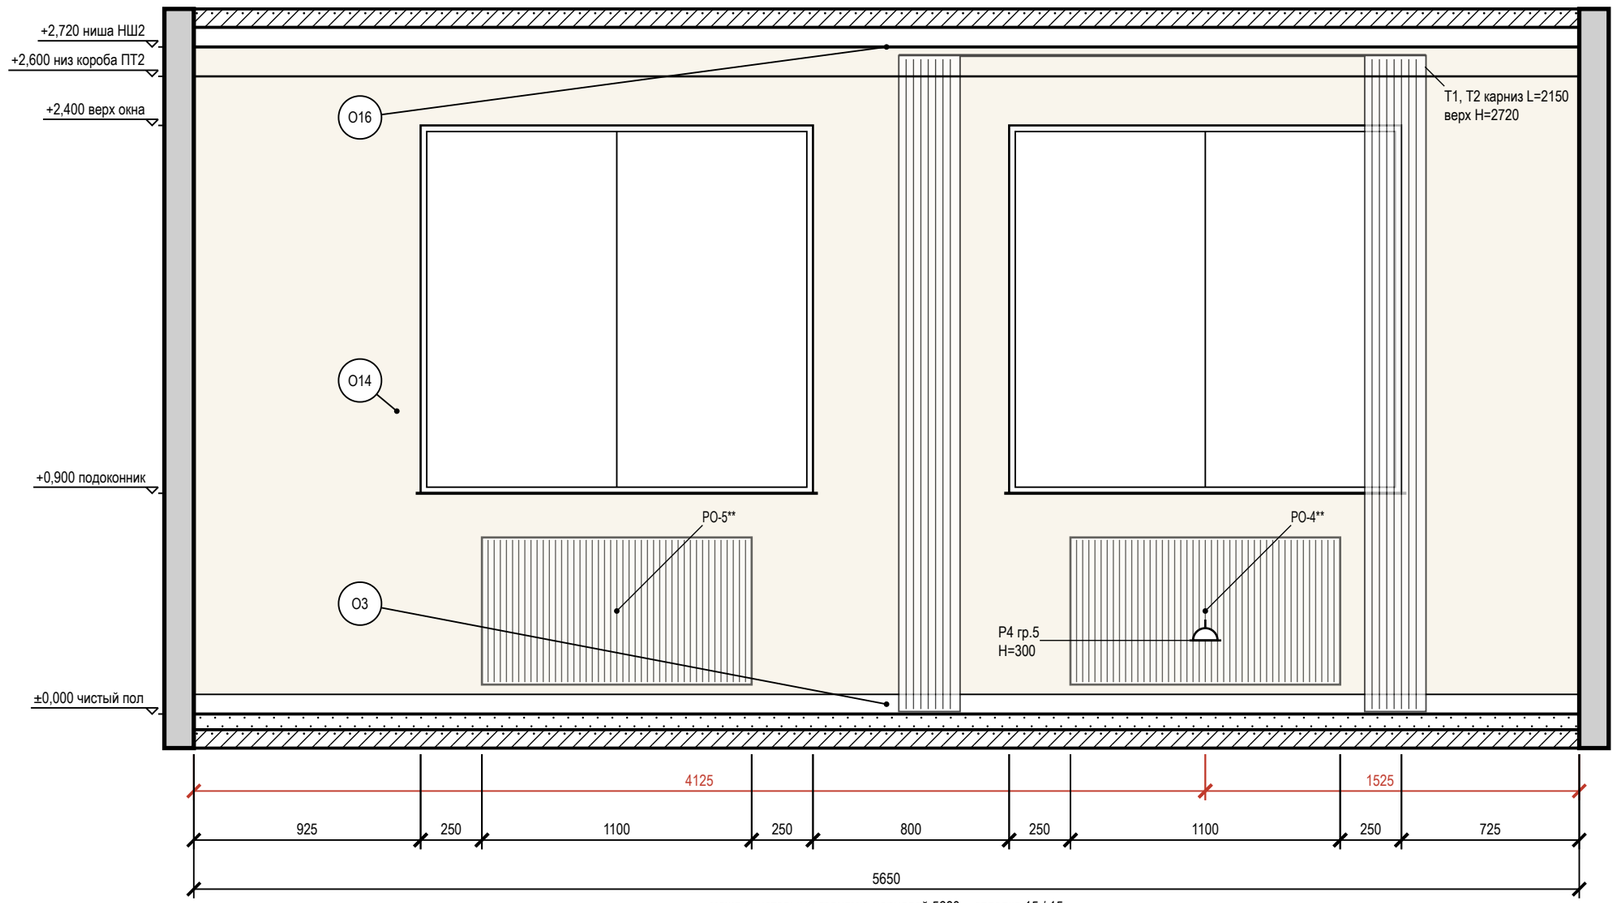

между чистовыми гранями: черновой 5680 − отделка 15 / 15

Схема развёрток (М 1:100)

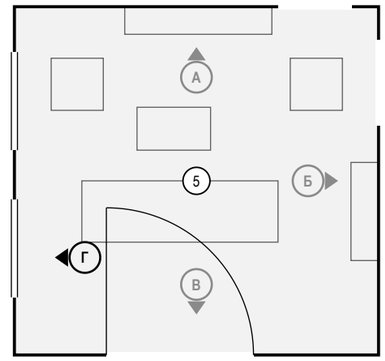

Условные обозначения

- розетка с заземляющим контактом; у знака — марка, ×N постов в рамке, гр. — группа щита, Н — высота оси, мм
- привязки точек и выводов от угла и от пола, мм
- мебель и приборы — фасад по расстановке (условно)
- карниз (шина) и шторы в собранном виде: марка Т, длина L, верх Н
- окно: проём, рама, подоконник
- радиатор отопления; марка — по плану отопления
- стены и перекрытия в сечении
- окраска: тон — цвет по коду производителя (условно)
- О1 — марка отделки по реестру отделки альбома
- А — марка развёртки: буква стены, стрелка — взгляд

Ведомость отделки (на листе)

Марка	Поверхность	Материал, изделие	Цвет, код	Кол.
О3	плинтус	плинтус МДФ, h 80 мм, аналог: плинтус МДФ под окраску 80×16 мм, полуглянцевая	NCS S 0804-Y30R «S 0804-Y30R»	5,7 м
О14	стены	окраска, Tikkurila Optiva 5 Matt, матовая, подготовка К3	NCS S 0804-Y30R «S 0804-Y30R»	10,6 м²
О16	потолок	окраска, Tikkurila Anti-Reflex 2, глубокоматовая, подготовка Q3	NCS S 0804-Y30R «S 0804-Y30R»	33,7 м²

Допущения и предложения на листе

Основа листа: размеры и контуры этажей подобраны проектировщиком по составу помещений и площадям этажей с картинки 470 px (размеры на ней не читаются); обмер и исходный проект — задание (К-1); высоты: 1-й этаж 2800 мм, мансарда 2700 мм (горизонтальная часть) приняты; скаты кровли мансарды приняты по картинке: колено 1200 мм, уклон 45°, конёк вдоль длинной стороны; проект КР — задание (К-2); наружные стены 400 мм, перегородки 120 мм приняты (К-1); разрешённая мощность 15 кВт принята по типовым ТУ для частного дома (К-4); подрайон климата не задан — принят не северный (жилые от 2,5 м) (К-7).

Знак «**» — предложение проектировщика, заказчиком не утверждено (согласовать с заказчиком): К-9: дверь пом. 5 (стена В) — проём 2400×2100 на веранду с картинки: одной распашной створкой не закрывается (полотна 600–900) — раздвижная двустворчатая, остеклённая; система и полотна — по каталогу после утверждения автором; К-11: РО-4, РО-5 — прибор под окном по оси проёма, ширина ≈ 0,7 ширины окна — предложение ОВ (лист ОВ выводил его сам до, теперь он в данных — один источник для листа, мебели, DXF и IFC); котёл и мощность не выбраны (К-11) — размер по теплотехническому расчёту.

См. лист открытых вопросов (лист 8, записи К-1, К-2, К-4, К-7; лист 9, записи К-9, К-11).

Примечания

1. Развёртки — вид на стену изнутри помещения, по часовой стрелке; расположение — на схеме листа и на листе 127; размеры — в мм по чистовым поверхностям; отметки — в м от ±0,000 (чистый пол 1-го этажа); высоты Н — от чистого пола помещения до оси изделия, у декора — до центра.
2. Красная цепочка — привязки электроточек и выводов по осям от угла чистовых стен; высота Н — у знака, от чистого пола до оси; высоты мебели, проёмов и границ отделки — колонкой отметок слева. Стена с 5 и более точками или с мелкими звеньями привязок показана двумя видами: архитектурная развёртка (мебель, отделка, проёмы, высоты) и вид «Привязки» на отдельном листе — точки и выводы с марками, одна цепочка по осям и таблица привязок (каждая точка — строка).
3. У знака электроточки: марка (Р — розетка, S — выключатель, Св — светильник, ЭВ — вывод кабеля), ×N — число постов в рамке, гр. — группа щита, Н — высота оси от чистого пола, мм; группы по клавишам выключателя — на листе выключателей.
4. Схема мебели, приборов и декора не является технической документацией для производства мебели; габариты — по паспортам изделий.
5. Карнизы (шины) — по ведомости текстиля декоратора: длина L и верх Н на развёртке — те же числа, что в ведомости; крепление — до окраски потолка.
6. Потолок — у каждой стены свой, по плану потолков (НШ2, ПТ2); ступени — зоной, кромка короба перед нишей — тонкой линией; в поле потолка: ПТ3 +2,700.

1000 мм · печать 1:1

Изм.	Кол.уч	Лист	№ док.	Подп.	Дата
Разраб.		Кырлан А.С.			04.11.26
Пров.					
ГИП					
Н. контр.					
Утв.					

ГД-2026-010-АИ

Дом 331 м²

Общая площадь 270,67* м² · * размеры приняты, не замерены (реестр — л. 8–10, К-1)

Дизайн-проект интерьера	Стадия	Лист	Листов
	РП	149	216

Развёртка стены Г. Гостиная (пом. 5)

М 1:25

Кырлан Александр Сергеевич

выпуск 04.11.2026 № 2a77323a49 · стр. 153 из 221

Развёртка стены А. Холл с лестницей (пом. 6)

Холл с лестницей (пом. 6) · вид изнутри помещения · размеры в мм, отметки в м от ±0,000 (чистый пол 1-го этажа)

Развёртка стены А


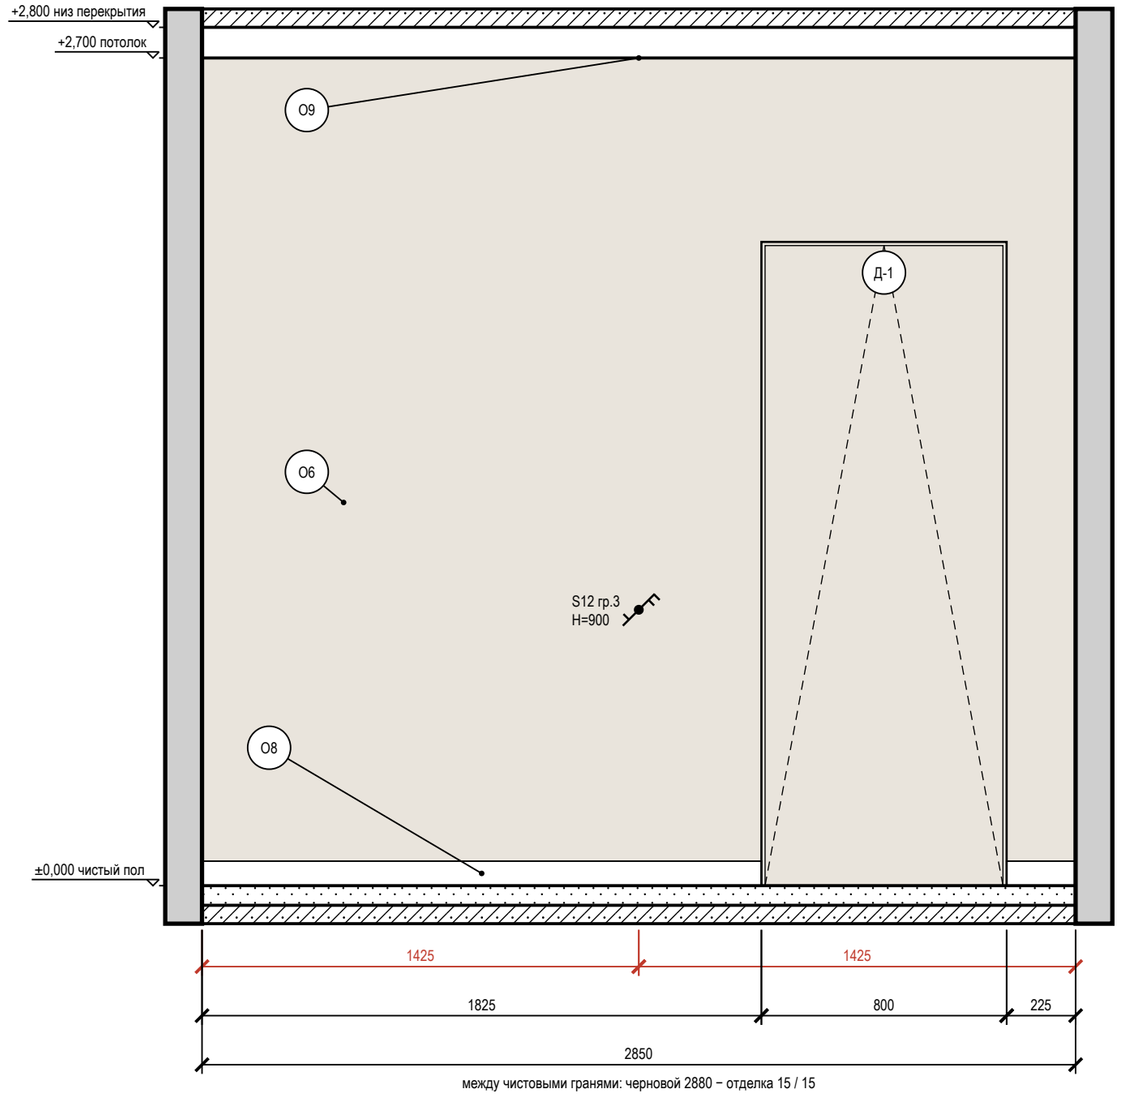


Схема развёрток (М 1:100)

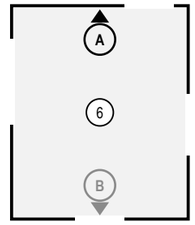

Условные обозначения

- выключатель одноклавишный
- выключатель двухклавишный (флажков — по числу клавиш)
- выключатель с проходной или перекрёстной клавишей (обратный флажок); тип клавиши — в подписи
- привязки точек и выводов от угла и от пола, мм
- мебель и приборы — фасад по расстановке (условно)
- дверь скрытого монтажа: полотно в плоскости стены (узел — на листе узлов)
- стены и перекрытия в сечении
- окраска: тон — цвет по коду производителя (условно)
- О1 — марка отделки по реестру отделки альбома
- А — марка развёртки: буква стены, стрелка — взгляд

Ведомость отделки (на листе)

Марка	Поверхность	Материал, изделие	Цвет, код	Кол.
О6	стены	окраска, Farrow & Ball Modern Emulsion, матовая, подготовка Q3	Farrow & Ball No. 226 «Joa's White»	6 м²
О8	плинтус	плинтус МДФ, h 80 мм, аналог: плинтус МДФ под покраску 80×16	Farrow & Ball No. 226 «Joa's White»	2 м
О9	потолок	окраска, Little Greene Absolute Matt, глубокоматовая, подготовка Q3	Little Greene No. 105 «Slaked Lime»	10 м²

Допущения и предложения на листе

Основа листа: размеры и контуры этажей подобраны проектировщиком по составу помещений и площадям этажей с картинки 470 px (размеры на ней не читаются); обмер и исходный проект — задание (К-1); высоты: 1-й этаж 2800 мм, мансарда 2700 мм (горизонтальная часть) приняты; скаты кровли мансарды приняты по картинке: колено 1200 мм, уклон 45°, конёк вдоль длинной стороны; проект КР — задание (К-2); наружные стены 400 мм, перегородки 120 мм приняты (К-1); разрешённая мощность 15 кВт принята по типовым ТУ для частного дома (К-4); подрайон климата не задан — принят не северный (жилые от 2,5 м) (К-7).

См. лист открытых вопросов (лист 8, записи К-1, К-2, К-4, К-7).

Примечания

1. Развёртки — вид на стену изнутри помещения, по часовой стрелке; расположение — на схеме листа и на листе 127; размеры — в мм по чистовым поверхностям; отметки — в м от ±0,000 (чистый пол 1-го этажа); высоты Н — от чистого пола помещения до оси изделия, у декора — до центра.
2. Красная цепочка — привязки электроточек и выводов по осям от угла чистовых стен; высота Н — у знака, от чистого пола до оси; высоты мебели, проёмов и границ отделки — колонкой отметок слева. Стена с 5 и более точками или с мелкими звеньями привязок показана двумя видами: архитектурная развёртка (мебель, отделка, проёмы, высоты) и вид «Привязки» на отдельном листе — точки и выводы с марками, одна цепочка по осям и таблица привязок (каждая точка — строка).
3. У знака электроточки: марка (Р — розетка, S — выключатель, Св — светильник, ЭВ — вывод кабеля), ×N — число постов в рамке, гр. — группа щита, Н — высота оси от чистого пола, мм; группы по клавишам выключателя — на листе выключателей.
4. Схема мебели, приборов и декора не является технической документацией для производства мебели; габариты — по паспортам изделий.
5. Двери скрытого монтажа — полотно в плоскости стены, отделка стены по полотну, плинтус прерывается у короба (узел — на листе узлов).

1000 мм · печать 1:1

Изм.	Кол.уч	Лист	№ док.	Подп.	Дата
Разраб.		Кырлан А.С.			04.11.26
Пров.					
ГИП					
Н. контр.					
Утв.					

ГД-2026-010-АИ

Дом 331 м²

Общая площадь 270,67* м² · * размеры приняты, не замерены (реестр — л. 8–10, К-1)

Дизайн-проект интерьера

Стадия	Лист	Листов
РП	150	216

Развёртка стены А. Холл с лестницей (пом. 6)

М 1:20

Кырлан Александр Сергеевич


выпуск 04.11.2026 № 2a77323a49 · стр. 154 из 221

Развёртка стены В. Холл с лестницей (пом. 6)

Холл с лестницей (пом. 6) · вид изнутри помещения · размеры в мм, отметки в м от ±0,000 (чистый пол 1-го этажа)


ПРЕДВАРИТЕЛЬНО · не для производства работ · открыто пунктов: 15 (реестр — л. 8–10)

Развёртка стены В

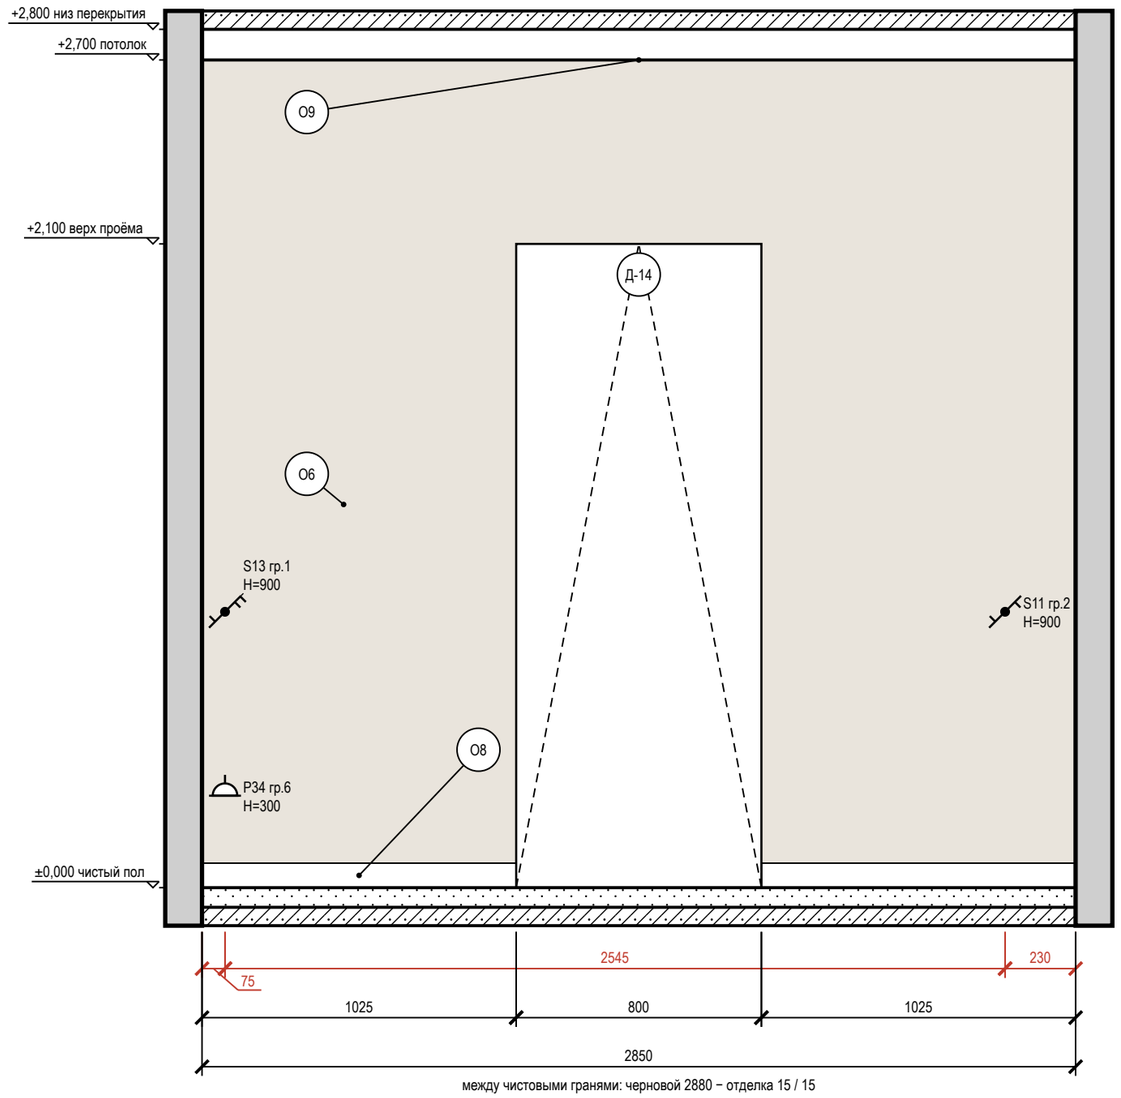

между чистовыми гранями: черновой 2880 − отделка 15 / 15

Схема развёрток (М 1:100)

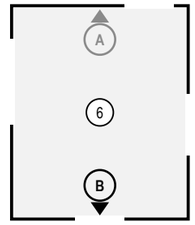

Условные обозначения

- розетка с заземляющим контактом; у знака — марка, ×N постов в рамке, гр. — группа щита, Н — высота оси, мм
- выключатель одноклавишный
- выключатель двухклавишный (флажков — по числу клавиш)
- выключатель с проходной или перекрёстной клавишей (обратный флажок); тип клавиши — в подписи
- привязки точек и выводов от угла и от пола, мм
- мебель и приборы — фасад по расстановке (условно)
- дверной проём; марка двери — в кружке
- стены и перекрытия в сечении
- окраска: тон — цвет по коду производителя (условно)
- О1 — марка отделки по реестру отделки альбома
- A — марка развёртки: буква стены, стрелка — взгляд

Ведомость отделки (на листе)

Марка	Поверхность	Материал, изделие	Цвет, код	Кол.
О6	стены	окраска, Farrow & Ball Modern Emulsion, матовая, подготовка Q3	Farrow & Ball No. 226 «Joa's White»	6 м²
О8	плинтус	плинтус МДФ, h 80 мм, аналог: плинтус МДФ под покраску 80×16	Farrow & Ball No. 226 «Joa's White»	2 м
О9	потолок	окраска, Little Greene Absolute Matt, глубокоматовая, подготовка Q3	Little Greene No. 105 «Slaked Lime»	10 м²

Допущения и предложения на листе

Основа листа: размеры и контуры этажей подобраны проектировщиком по составу помещений и площадям этажей с картинки 470 px (размеры на ней не читаются); обмер и исходный проект — задание (К-1); высоты: 1-й этаж 2800 мм, мансарда 2700 мм (горизонтальная часть) приняты; скаты кровли мансарды приняты по картинке: колено 1200 мм, уклон 45°, конёк вдоль длинной стороны; проект КР — задание (К-2); наружные стены 400 мм, перегородки 120 мм приняты (К-1); разрешённая мощность 15 кВт принята по типовым ТУ для частного дома (К-4); подрайон климата не задан — принят не северный (жилые от 2,5 м) (К-7).

См. лист открытых вопросов (лист 8, записи К-1, К-2, К-4, К-7).

Примечания

1. Развёртки — вид на стену изнутри помещения, по часовой стрелке; расположение — на схеме листа и на листе 127; размеры — в мм по чистовым поверхностям; отметки — в м от ±0,000 (чистый пол 1-го этажа); высоты Н — от чистого пола помещения до оси изделия, у декора — до центра.
2. Красная цепочка — привязки электроточек и выводов по осям от угла чистовых стен; высота Н — у знака, от чистого пола до оси; высоты мебели, проёмов и границ отделки — колонкой отметок слева. Стена с 5 и более точками или с мелкими звеньями привязок показана двумя видами: архитектурная развёртка (мебель, отделка, проёмы, высоты) и вид «Привязки» на отдельном листе — точки и выводы с марками, одна цепочка по осям и таблица привязок (каждая точка — строка).
3. У знака электроточки: марка (Р — розетка, S — выключатель, Св — светильник, ЭВ — вывод кабеля), ×N — число постов в рамке, гр. — группа щита, Н — высота оси от чистого пола, мм; группы по клавишам выключателя — на листе выключателей.
4. Схема мебели, приборов и декора не является технической документацией для производства мебели; габариты — по паспортам изделий.

1000 мм · печать 1:1

Изм.	Кол.уч	Лист	№ док.	Подп.	Дата
Разраб.		Кырлан А.С.			04.11.26
Пров.					
ГИП					
Н. контр.					
Утв.					

ГД-2026-010-АИ

Дом 331 м²

Общая площадь 270,67* м² · * размеры приняты, не замерены (реестр — л. 8–10, К-1)

Дизайн-проект интерьера

Стадия	Лист	Листов
РП	151	216

Развёртка стены В. Холл с лестницей (пом. 6)

М 1:20


Кырлан Александр Сергеевич

выпуск 04.11.2026 № 2a77323a49 · стр. 155 из 221

Развёртки стен. Кладовая (пом. 7)


Кладовая (пом. 7) · вид изнутри помещения · размеры в мм, отметки в м от ±0,000 (чистый пол 1-го этажа)

Развёртка стены В

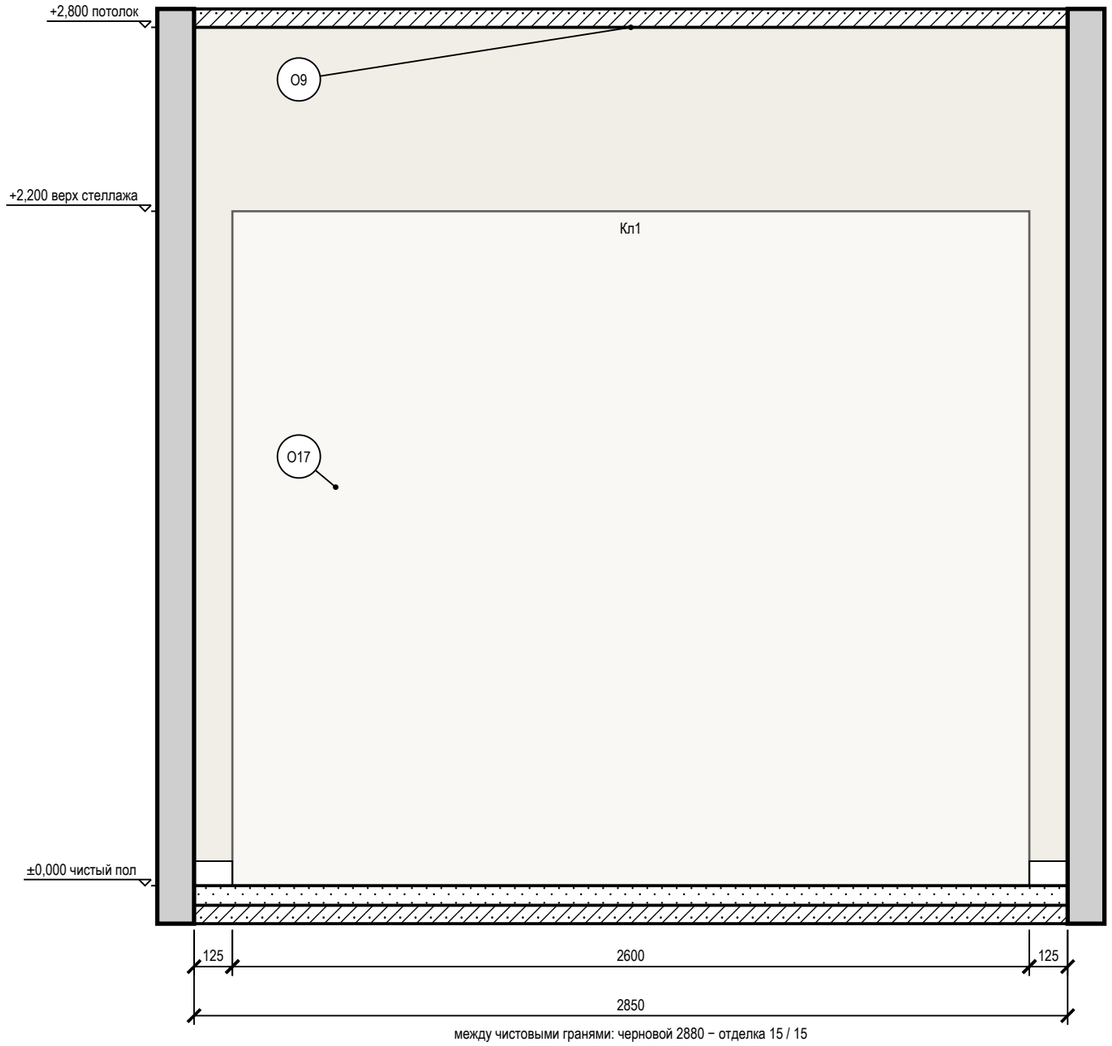

между чистовыми гранями: черновой 2880 − отделка 15 / 15

Схема развёрток (М 1:100)

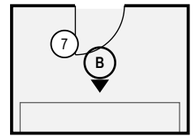

Условные обозначения

- мебель и приборы — фасад по расстановке (условно)
- стены и перекрытия в сечении
- окраска: тон — цвет по коду производителя (условно)
- О1 — марка отделки по реестру отделки альбома
- А — марка развёртки: буква стены, стрелка — взгляд

Ведомость отделки (на листе)

Марка	Поверхность	Материал, изделие	Цвет, код	Кол.
О9	потолок	окраска, Little Greene Absolute Matt, глубокоматовая, подготовка Q3	Little Greene No. 105 «Slaked Lime»	6 м²
О17	стены	окраска, Little Greene Intelligent Matt, матовая, подготовка Q3	Little Greene No. 105 «Slaked Lime»	8 м²
О18	плинтус	плинтус МДФ, h 80 мм, аналог: плинтус МДФ под покраску 80×16	Little Greene No. 105 «Slaked Lime»	0,3 м

Примечания

1. Развёртки — вид на стену изнутри помещения, по часовой стрелке; расположение — на схеме листа и на листе 127; размеры — в мм по чистовым поверхностям; отметки — в м от ±0,000 (чистый пол 1-го этажа); высоты Н — от чистого пола помещения до оси изделия, у декора — до центра.
2. Схема мебели, приборов и декора не является технической документацией для производства мебели; габариты — по паспортам изделий.

Допущения и предложения на листе

Основа листа: размеры и контуры этажей подобраны проектировщиком по составу помещений и площадям этажей с картинки 470 px (размеры на ней не читаются); обмер и исходный проект — задание (К-1); высоты: 1-й этаж 2800 мм, мансарда 2700 мм (горизонтальная часть) приняты; скаты кровли мансарды приняты по картинке: колено 1200 мм, уклон 45°, конёк вдоль длинной стороны; проект КР — задание (К-2); наружные стены 400 мм, перегородки 120 мм приняты (К-1); разрешённая мощность 15 кВт принята по типовым ТУ для частного дома (К-4); подрайон климата не задан — принят не северный (жилые от 2,5 м) (К-7).

См. лист открытых вопросов (лист 8, записи К-1, К-2, К-4, К-7).

1000 мм · печать 1:1

Изм.	Кол.уч	Лист	№ док.	Подп.	Дата
Разраб.		Кырлан А.С.			04.11.26
Пров.					
ГИП					
Н. контр.					
Утв.					

ГД-2026-010-АИ

Дом 331 м²

Общая площадь 270,67* м² · * размеры приняты, не замерены (реестр — л. 8–10, К-1)

Дизайн-проект интерьера

Стадия	Лист	Листов
РП	152	216

Развёртки стен. Кладовая (пом. 7)

М 1:20


Кырлан Александр Сергеевич

выпуск 04.11.2026 № 2a77323a49 · стр. 156 из 221

Развёртка стены А. Прихожая (пом. 8)


Прихожая (пом. 8) · вид изнутри помещения · размеры в мм, отметки в м от ±0,000 (чистый пол 1-го этажа)

Развёртка стены А

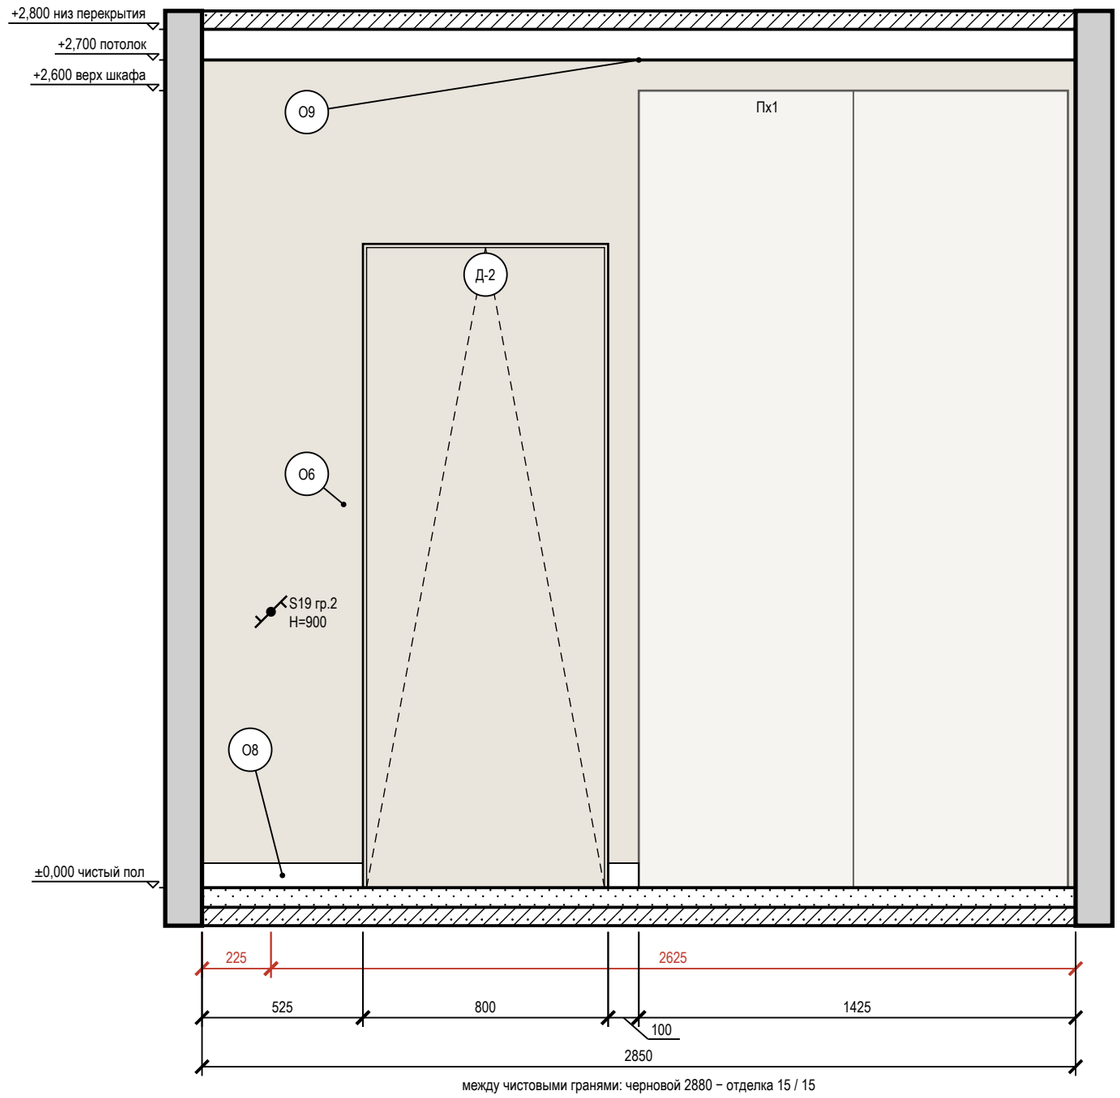

между чистовыми гранями: черновой 2880 − отделка 15 / 15

Схема развёрток (М 1:100)

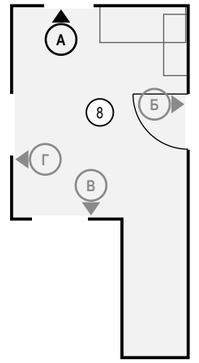

Допущения и предложения на листе

Основа листа: размеры и контуры этажей подобраны проектировщиком по составу помещений и площадям этажей с картинки 470 px (размеры на ней не читаются); обмер и исходный проект — задание (К-1); высоты: 1-й этаж 2800 мм, мансарда 2700 мм (горизонтальная часть) приняты; скаты кровли мансарды приняты по картинке: колено 1200 мм, уклон 45°, конёк вдоль длинной стороны; проект КР — задание (К-2); наружные стены 400 мм, перегородки 120 мм приняты (К-1); разрешённая мощность 15 кВт принята по типовым ТУ для частного дома (К-4); подрайон климата не задан — принят не северный (жилые от 2,5 м) (К-7).

Знак «**» — предложение проектировщика, заказчиком не утверждено (согласовать с заказчиком): дверь пом. 8 (стена Б) — дверь гаража в дом — СП 55.13330.2016 п. 7.7: EI 30, уплотнение в притворах, самозакрывание (доводчик).

См. лист открытых вопросов (лист 8, записи К-1, К-2, К-4, К-7).

Условные обозначения

- выключатель одноклавишный
- выключатель с проходной или перекрёстной клавишей (обратный флажок); тип клавиши — в подписи
- привязки точек и выводов от угла и от пола, мм
- мебель и приборы — фасад по расстановке (условно)
- дверь скрытого монтажа: полотно в плоскости стены (узел — на листе узлов)
- стены и перекрытия в сечении
- окраска: тон — цвет по коду производителя (условно)
- О1 — марка отделки по реестру отделки альбома
- А — марка развёртки: буква стены, стрелка — взгляд

Ведомость отделки (на листе)

Марка	Поверхность	Материал, изделие	Цвет, код	Кол.
О6	стены	окраска, Farrow & Ball Modern Emulsion, матовая, подготовка Q3	Farrow & Ball No. 226 «Joa's White»	6 м²
О8	плинтус	плинтус МДФ, h 80 мм, аналог: плинтус МДФ под покраску 80×16	Farrow & Ball No. 226 «Joa's White»	0,6 м
О9	потолок	окраска, Little Greene Absolute Matt, глубокоматовая, подготовка Q3	Little Greene No. 105 «Slaked Lime»	12,5 м²

Примечания

1. Развёртки — вид на стену изнутри помещения, по часовой стрелке; расположение — на схеме листа и на листе 127; размеры — в мм по чистовым поверхностям; отметки — в м от ±0,000 (чистый пол 1-го этажа); высоты Н — от чистого пола помещения до оси изделия, у декора — до центра.
2. Красная цепочка — привязки электроточек и выводов по осям от угла чистовых стен; высота Н — у знака, от чистого пола до оси; высоты мебели, проёмов и границ отделки — колонкой отметок слева. Стена с 5 и более точками или с мелкими звеньями привязок показана двумя видами: архитектурная развёртка (мебель, отделка, проёмы, высоты) и вид «Привязки» на отдельном листе — точки и выводы с марками, одна цепочка по осям и таблица привязок (каждая точка — строка).
3. У знака электроточки: марка (Р — розетка, S — выключатель, Св — светильник, ЭВ — вывод кабеля), ×N — число постов в рамке, гр. — группа щита, Н — высота оси от чистого пола, мм; группы по клавишам выключателя — на листе выключателей.
4. Схема мебели, приборов и декора не является технической документацией для производства мебели; габариты — по паспортам изделий.
5. Двери скрытого монтажа — полотно в плоскости стены, отделка стены по полотну, плинтус прерывается у короба (узел — на листе узлов).

1000 мм · печать 1:1

Изм.	Кол.уч	Лист	№ док.	Подп.	Дата			
Разраб.		Кырлан А.С.			04.11.26	ГД-2026-010-АИ		
Пров.						Дом 331 м²		
ГИП						Общая площадь 270,67* м² · * размеры приняты, не замерены (реестр — л. 8–10, К-1)		
Н. контр.						Дизайн-проект интерьера	Стадия: РП	Лист: 153 / Листов: 216
Утв.						Развёртка стены А. Прихожая (пом. 8) · М 1:20	Кырлан Александр Сергеевич	


выпуск 04.11.2026 № 2a77323a49 · стр. 157 из 221

Развёртка стены Б. Прихожая (пом. 8)

Прихожая (пом. 8) · вид изнутри помещения · размеры в мм, отметки в м от ±0,000 (чистый пол 1-го этажа)


ПРЕДВАРИТЕЛЬНО · не для производства работ · открыто пунктов: 15 (реестр — л. 8–10)

Развёртка стены Б

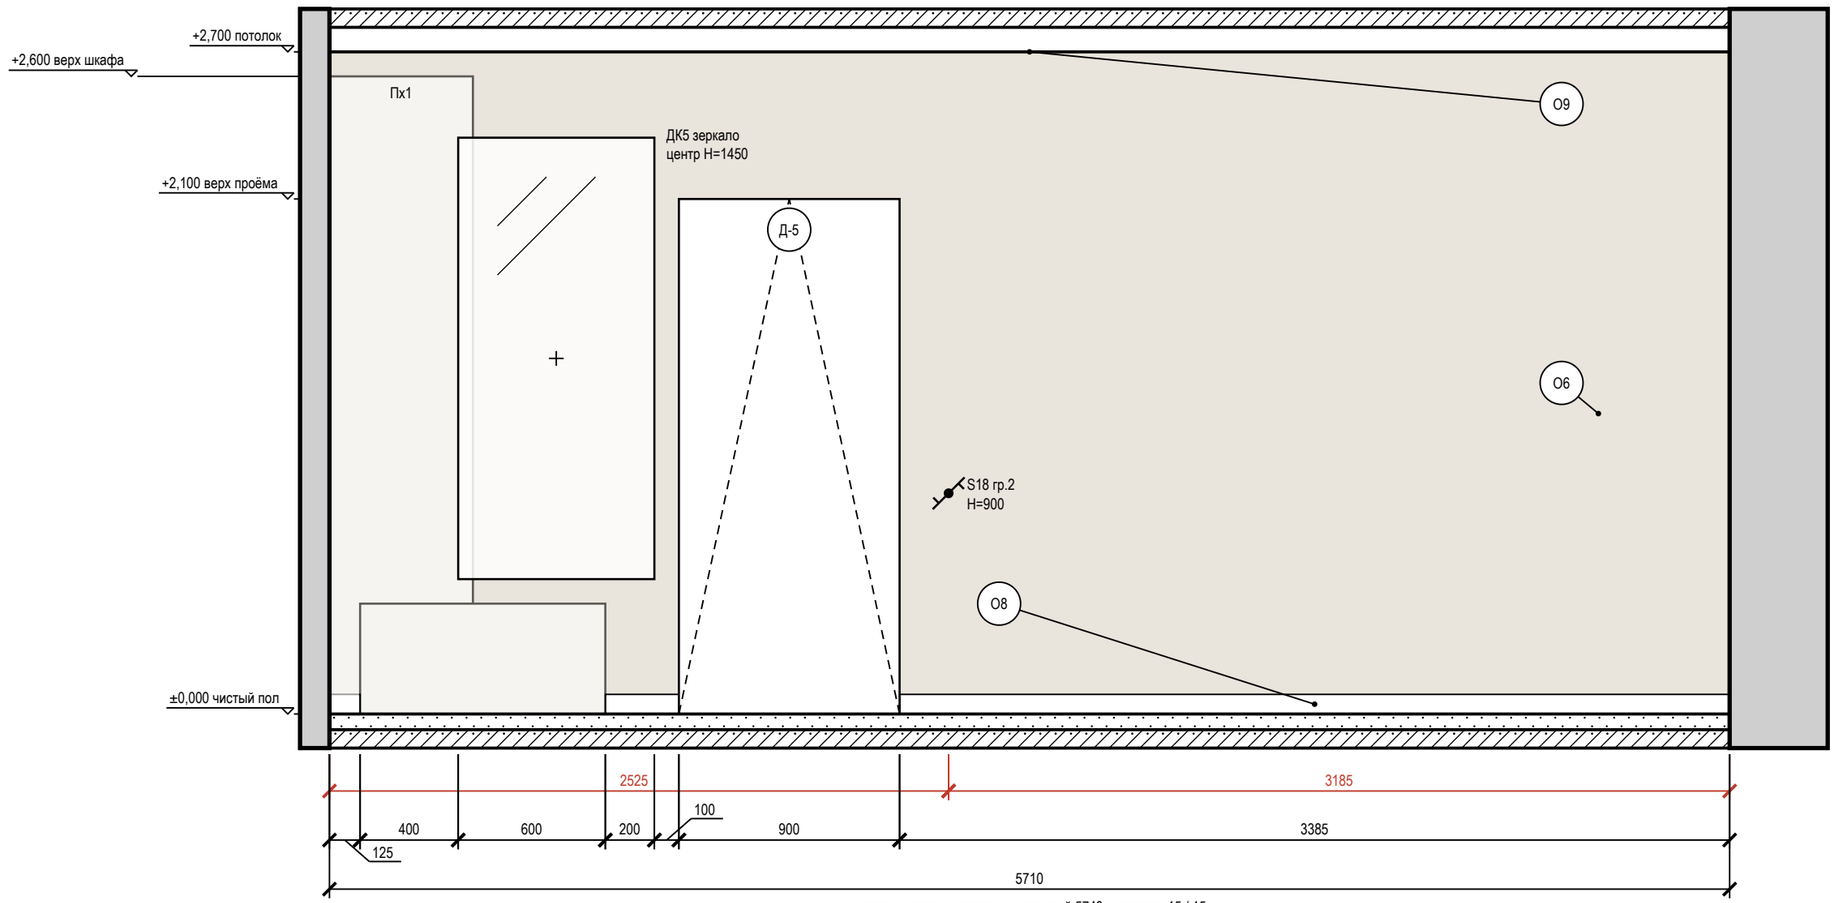

между чистовыми гранями: черновой 5740 − отделка 15 / 15

Схема развёрток (М 1:100)

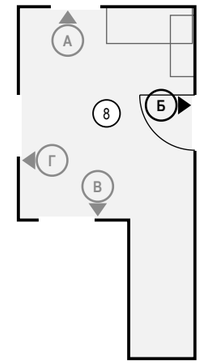

Допущения и предложения на листе

Основа листа: размеры и контуры этажей подобраны проектировщиком по составу помещений и площадям этажей с картинки 470 px (размеры на ней не читаются); обмер и исходный проект — задание (К-1); высоты: 1-й этаж 2800 мм, мансарда 2700 мм (горизонтальная часть) приняты; скаты кровли мансарды приняты по картинке: колено 1200 мм, уклон 45°, конёк вдоль длинной стороны; проект КР — задание (К-2); наружные стены 400 мм, перегородки 120 мм приняты (К-1); разрешённая мощность 15 кВт принята по типовым ТУ для частного дома (К-4); подрайон климата не задан — принят не северный (жилые от 2,5 м) (К-7).

Знак «**» — предложение проектировщика, заказчиком не утверждено (согласовать с заказчиком): дверь пом. 8 (стена Б) — дверь гаража в дом — СП 55.13330.2016 п. 7.7: EI 30, уплотнение в притворах, самозакрывание (доводчик).

См. лист открытых вопросов (лист 8, записи К-1, К-2, К-4, К-7).

Условные обозначения

- выключатель одноклавишный
- выключатель с проходной или перекрёстной клавишей (обратный флажок); тип клавиши — в подписи
- привязки точек и выводов от угла и от пола, мм
- мебель и приборы — фасад по расстановке (условно)
- зеркало: марка Д, крест — центр, Н — высота центра, мм
- дверной проём; марка двери — в кружке
- стены и перекрытия в сечении
- окраска: тон — цвет по коду производителя (условно)
- О1 — марка отделки по реестру отделки альбома
- А — марка развёртки: буква стены, стрелка — взгляд

Ведомость отделки (на листе)

Марка	Поверхность	Материал, изделие	Цвет, код	Кол.
О6	стены	окраска, Farrow & Ball Modern Emulsion, матовая, подготовка Q3	Farrow & Ball No. 226 «Joa's White»	13,5 м²
О8	плинтус	плинтус МДФ, h 80 мм, аналог: плинтус МДФ под покраску 80×16	Farrow & Ball No. 226 «Joa's White»	3,8 м
О9	потолок	окраска, Little Greene Absolute Matt, глубокоматовая, подготовка Q3	Little Greene No. 105 «Slaked Lime»	12,5 м²

Примечания

1. Развёртки — вид на стену изнутри помещения, по часовой стрелке; расположение — на схеме листа и на листе 127; размеры — в мм по чистовым поверхностям; отметки — в м от ±0,000 (чистый пол 1-го этажа); высоты Н — от чистого пола помещения до оси изделия, у декора — до центра.
2. Красная цепочка — привязки электроточек и выводов по осям от угла чистовых стен; высота Н — у знака, от чистого пола до оси; высоты мебели, проёмов и границ отделки — колонкой отметок слева. Стена с 5 и более точками или с мелкими звеньями привязок показана двумя видами: архитектурная развёртка (мебель, отделка, проёмы, высоты) и вид «Привязки» на отдельном листе — точки и выводы с марками, одна цепочка по осям и таблица привязок (каждая точка — строка).
3. У знака электроточки: марка (Р — розетка, S — выключатель, Св — светильник, ЭВ — вывод кабеля), ×N — число постов в рамке, гр. — группа щита, Н — высота оси от чистого пола, мм; группы по клавишам выключателя — на листе выключателей.
4. Схема мебели, приборов и декора не является технической документацией для производства мебели; габариты — по паспортам изделий.
5. Картины и зеркала крепить к основанию по паспорту изделия (закладные и анкеры — в перечне скрытых работ); крест — ось центра предмета.

1000 мм · печать 1:1

Изм.	Кол.уч	Лист	№ док.	Подп.	Дата			
Разраб.		Кырлан А.С.			04.11.26	ГД-2026-010-АИ		
Пров.						Дом 331 м²		
ГИП						Общая площадь 270,67* м² · * размеры приняты, не замерены (реестр — л. 8–10, К-1)		
						Дизайн-проект интерьера	Стадия: РП	Лист: 154 / Листов: 216
Н. контр.						Развёртка стены Б. Прихожая (пом. 8)	Кырлан Александр Сергеевич	
Утв.						М 1:25		


выпуск 04.11.2026 № 2a77323a49 · стр. 158 из 221

Развёртки стен В, Г. Прихожая (пом. 8)

Прихожая (пом. 8) · вид изнутри помещения · размеры в мм, отметки в м от ±0,000 (чистый пол 1-го этажа)


ПРЕДВАРИТЕЛЬНО · не для производства работ · открыто пунктов: 15 (реестр — л. 8–10)

Развёртка стены В

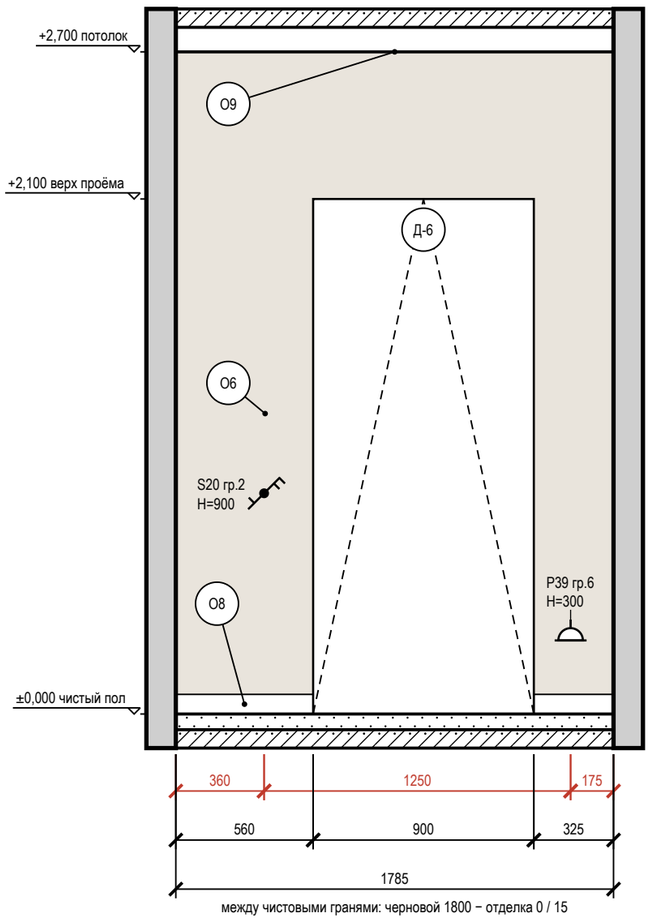


между чистовыми гранями: черновой 1800 − отделка 0 / 15

Развёртка стены Г

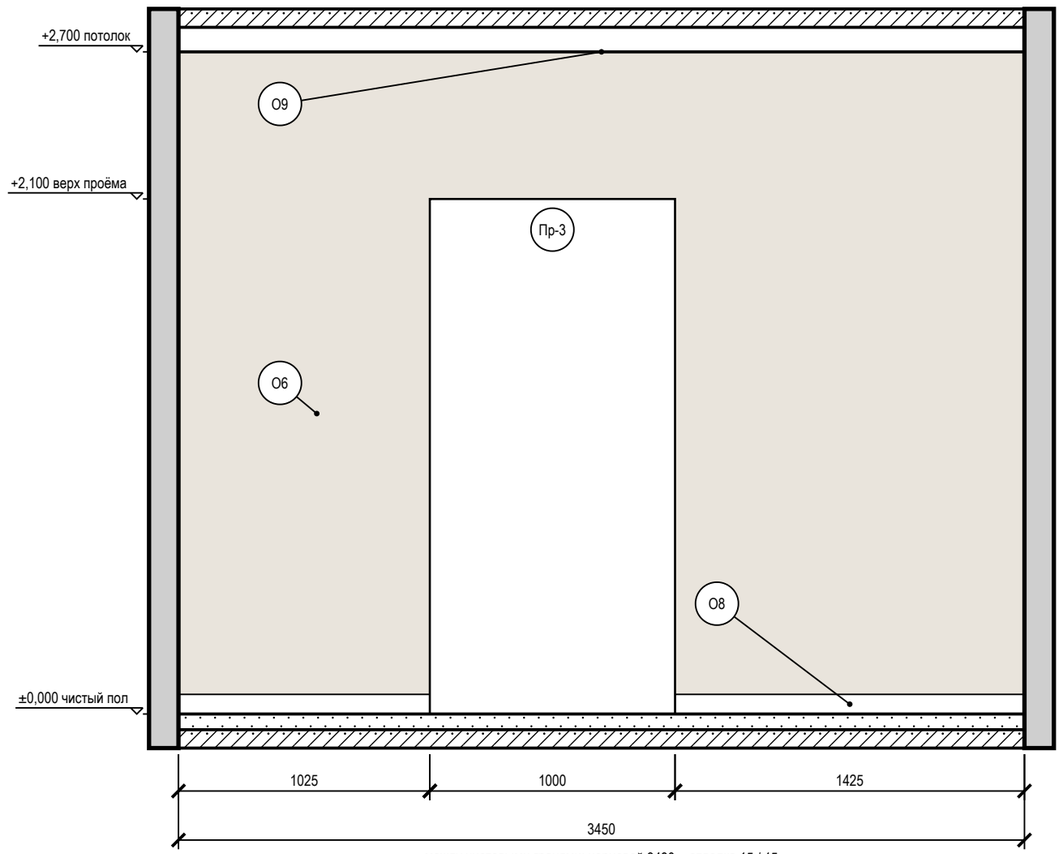

между чистовыми гранями: черновой 3480 − отделка 15 / 15

Схема развёрток (М 1:100)

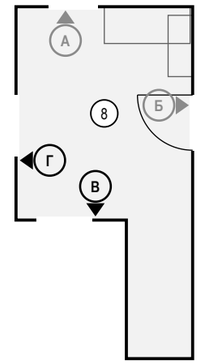

Условные обозначения

- розетка с заземляющим контактом; у знака — марка, ×N постов в рамке, гр. — группа щита, Н — высота оси, мм
- выключатель одноклавишный
- выключатель двухклавишный (флажков — по числу клавиш)
- выключатель с проходной или перекрёстной клавишей (обратный флажок); тип клавиши — в подписи
- привязки точек и выводов от угла и от пола, мм
- мебель и приборы — фасад по расстановке (условно)
- дверной проём; марка двери — в кружке
- стены и перекрытия в сечении
- окраска: тон — цвет по коду производителя (условно)
- О1 — марка отделки по реестру отделки альбома
- А — марка развёртки: буква стены, стрелка — взгляд

Ведомость отделки (на листе)

Марка	Поверхность	Материал, изделие	Цвет, код	Кол.
О6	стены	окраска, Farrow & Ball Modern Emulsion, матовая, подготовка Q3	Farrow & Ball No. 226 «Joa's White»	10,1 м²
О8	плинтус	плинтус МДФ, h 80 мм, аналог: плинтус МДФ под покраску 80×16	Farrow & Ball No. 226 «Joa's White»	3,3 м
О9	потолок	окраска, Little Greene Absolute Matt, глубокоматовая, подготовка Q3	Little Greene No. 105 «Slaked Lime»	12,5 м²

Примечания

1. Развёртки — вид на стену изнутри помещения, по часовой стрелке; расположение — на схеме листа и на листе 127; размеры — в мм по чистовым поверхностям; отметки — в м от ±0,000 (чистый пол 1-го этажа); высоты Н — от чистого пола помещения до оси изделия, у декора — до центра.
2. Красная цепочка — привязки электроточек и выводов по осям от угла чистовых стен; высота Н — у знака, от чистого пола до оси; высоты мебели, проёмов и границ отделки — колонкой отметок слева. Стена с 5 и более точками или с мелкими звеньями привязок показана двумя видами: архитектурная развёртка (мебель, отделка, проёмы, высоты) и вид «Привязки» на отдельном листе — точки и выводы с марками, одна цепочка по осям и таблица привязок (каждая точка — строка).
3. Стена Г показана двумя видами: здесь — архитектурная развёртка (мебель, отделка, проёмы, высоты), электроточки и выводы ВК с привязками и таблицей — на листе 156 («Привязки»).
4. У знака электроточки: марка (Р — розетка, S — выключатель, Св — светильник, ЭВ — вывод кабеля), ×N — число постов в рамке, гр. — группа щита, Н — высота оси от чистого пола, мм; группы по клавишам выключателя — на листе выключателей.
5. Схема мебели, приборов и декора не является технической документацией для производства мебели; габариты — по паспортам изделий.

1000 мм · печать 1:1

Допущения и предложения на листе

Основа листа: размеры и контуры этажей подобраны проектировщиком по составу помещений и площадям этажей с картинки 470 px (размеры на ней не читаются); обмер и исходный проект — задание (К-1); высоты: 1-й этаж 2800 мм, мансарда 2700 мм (горизонтальная часть) приняты; скаты кровли мансарды приняты по картинке: колено 1200 мм, уклон 45°, конёк вдоль длинной стороны; проект КР — задание (К-2); наружные стены 400 мм, перегородки 120 мм приняты (К-1); разрешённая мощность 15 кВт принята по типовым ТУ для частного дома (К-4); подрайон климата не задан — принят не северный (жилые от 2,5 м) (К-7).

Знак «**» — предложение проектировщика, заказчиком не утверждено (согласовать с заказчиком): дверь пом. 8 (стена Б) — дверь гаража в дом — СП 55.13330.2016 п. 7.7: EI 30, уплотнение в притворах, самозакрывание (доводчик).

См. лист открытых вопросов (лист 8, записи К-1, К-2, К-4, К-7).

Изм.	Кол.уч	Лист	№ док.	Подп.	Дата
Разраб.		Кырлан А.С.			04.11.26
Пров.					
ГИП					
Н. контр.					
Утв.					

ГД-2026-010-АИ

Дом 331 м²

Общая площадь 270,67* м² · * размеры приняты, не замерены (реестр — л. 8–10, К-1)

Дизайн-проект интерьера

Стадия	Лист	Листов
РП	155	216

Развёртки стен В, Г. Прихожая (пом. 8)

М 1:25

Кырлан Александр Сергеевич

выпуск 04.11.2026 № 2a77323a49 · стр. 159 из 221

Привязки электроточек, стена Г. Прихожая (пом. 8)

Прихожая (пом. 8) · вид изнутри помещения · привязки в мм, отметки в м · к развёртке на листе 155

ПРЕДВАРИТЕЛЬНО · не для производства работ · открыто пунктов: 15 (реестр — л. 8–10)

Развёртка стены Г: электроточки и выводы

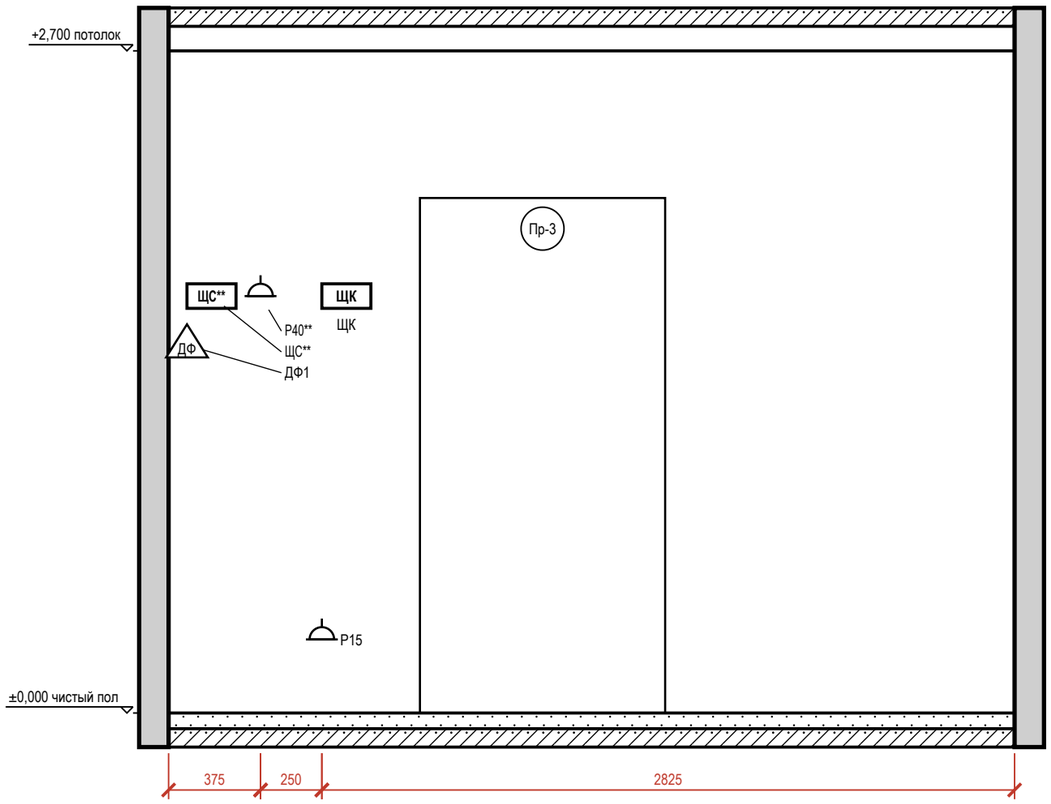



Таблица привязок электроточек и выводов

Марка	Назначение	От угла, мм	Н от пола, мм	Примечание
ДФ1	домофон: трубка домофона	75	1500	
ЩС**	щит: щит слаботочный: ввод оптики, ONT, роутер, патч-панель	175	1700	
Р40**	розетка: питание слаботочного щита (рядом с ЩС**)	375	1700	гр. 14
Р15	розетка: пылесос, сушилка обуви	625	300	гр. 6
ЩК	щит: щит квартирный ЩРВ-П-48	725	1700	

Условные обозначения

- розетка с заземляющим контактом; у знака — марка, ×N постов в рамке, гр. — группа щита, Н — высота оси, мм
- ДФ — трубка или монитор домофона
- ЩК — щит квартирный
- привязки точек и выводов от угла и от пола, мм
- А — марка развёртки: буква стены, стрелка — взгляд

Схема развёрток (М 1:100)

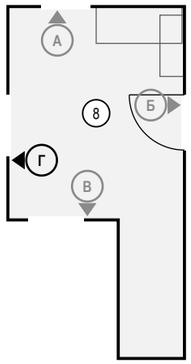

Примечания

1. Вид «Привязки» стены Г — электроточки и выводы ВК; архитектурная развёртка (мебель, отделка, проёмы, высоты) — на листе 155, расположение — на листе 127. Мебель и приборы — подложкой для ориентира; их марки и обозначения мебели, проёмов и стен — там же.
2. Привязки — в мм: по горизонтали от левого чистового угла стены до оси изделия, Н — от чистого пола до оси; все точки — в таблице привязок. Красная цепочка — привязки по осям; точки ближе 150 мм одна к другой в цепочку не дробятся — их привязки только в таблице.
3. У знака — марка электроточки (Р — розетка, S — выключатель, Св — светильник, ЭВ — вывод кабеля); посты в рамке и группа щита — в графе «Примечание»; группы по клавишам выключателя — на листе выключателей.

Допущения и предложения на листе

Основа листа: размеры и контуры этажей подобраны проектировщиком по составу помещений и площадям этажей с картинки 470 px (размеры на ней не читаются); обмер и исходный проект — задание (К-1); высоты: 1-й этаж 2800 мм, мансарда 2700 мм (горизонтальная часть) приняты; скаты кровли мансарды приняты по картинке: колено 1200 мм, уклон 45°, конёк вдоль длинной стороны; проект КР — задание (К-2); наружные стены 400 мм, перегородки 120 мм приняты (К-1); разрешённая мощность 15 кВт принята по типовым ТУ для частного дома (К-4); подрайон климата не задан — принят не северный (жилые от 2,5 м) (К-7).

Знак «**» — предложение проектировщика, заказчиком не утверждено (согласовать с заказчиком): Р40 — высота 1700 мм выше нормы 1 м (ПУЭ 6.6.30) по назначению: питание слаботочного щита ЩС, рядом со щитом на его высоте; ЩС — щит слаботочный: место и состав; дверь пом. 8 (стена Б) — дверь гаража в дом — СП 55.13330.2016 п. 7.7: EI 30, уплотнение в притворах, самозакрывание (доводчик).

См. лист открытых вопросов (лист 8, записи К-1, К-2, К-4, К-7).

1000 мм · печать 1:1

Изм.	Кол.уч	Лист	№ док.	Подп.	Дата
Разраб.		Кырлан А.С.			04.11.26
Пров.					
ГИП					
Н. контр.					
Утв.					

ГД-2026-010-АИ

Дом 331 м²

Общая площадь 270,67* м² · * размеры приняты, не замерены (реестр — л. 8–10, К-1)

Дизайн-проект интерьера

Стадия	Лист	Листов
РП	156	216

Привязки электроточек, стена Г. Прихожая (пом. 8)

М 1:25

Кырлан Александр Сергеевич


выпуск 04.11.2026 № 2a77323a49 · стр. 160 из 221

Развёртки стен. Тамбур (пом. 9)

Тамбур (пом. 9) · вид изнутри помещения · размеры в мм, отметки в м от ±0,000 (чистый пол 1-го этажа)


ПРЕДВАРИТЕЛЬНО · не для производства работ · открыто пунктов: 15 (реестр — л. 8–10)

Развёртка стены Г

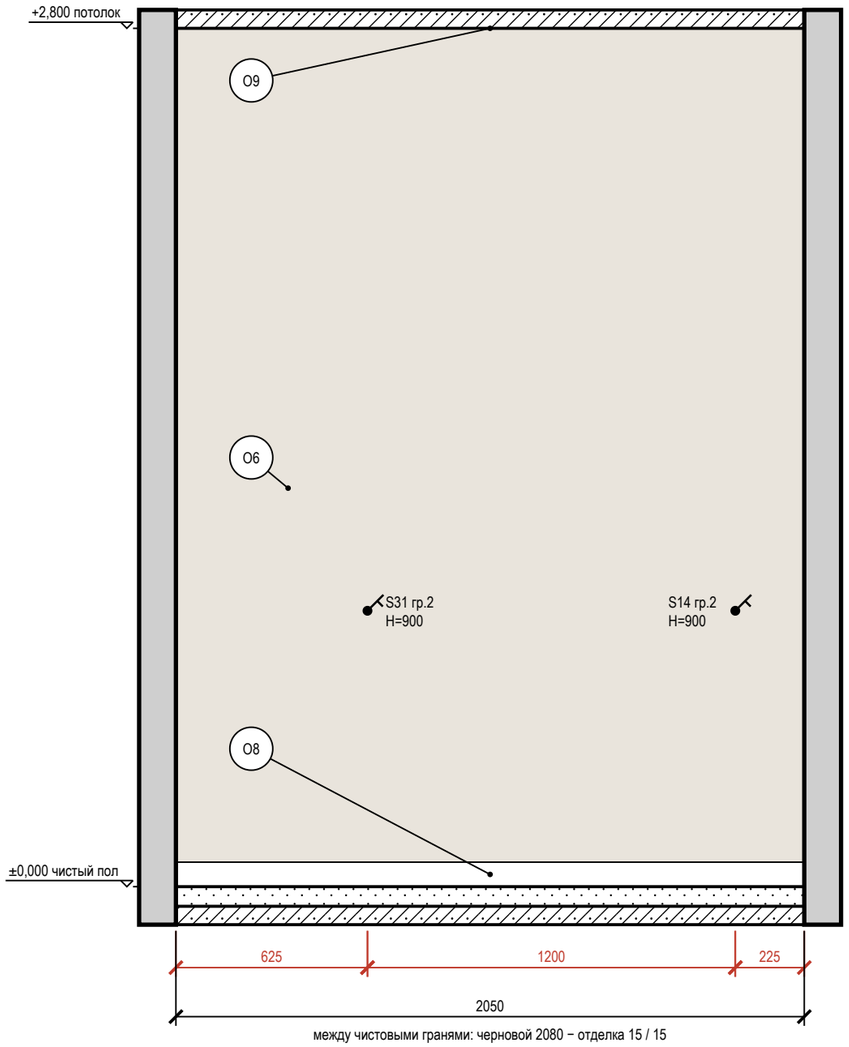

между чистовыми гранями: черновой 2080 − отделка 15 / 15

Схема развёрток (М 1:100)

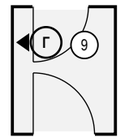

Условные обозначения

- выключатель одноклавишный
- привязки точек и выводов от угла и от пола, мм
- мебель и приборы — фасад по расстановке (условно)
- стены и перекрытия в сечении
- окраска: тон — цвет по коду производителя (условно)
- О1 — марка отделки по реестру отделки альбома
- А — марка развёртки: буква стены, стрелка — взгляд

Ведомость отделки (на листе)

Марка	Поверхность	Материал, изделие	Цвет, код	Кол.
О6	стены	окраска, Farrow & Ball Modern Emulsion, матовая, подготовка Q3	Farrow & Ball No. 226 «Joa's White»	5,7 м²
О8	плинтус	плинтус МДФ, h 80 мм, аналог: плинтус МДФ под покраску 80×16	Farrow & Ball No. 226 «Joa's White»	2 м
О9	потолок	окраска, Little Greene Absolute Matt, глубокоматовая, подготовка Q3	Little Greene No. 105 «Slaked Lime»	3,5 м²

Допущения и предложения на листе

Основа листа: размеры и контуры этажей подобраны проектировщиком по составу помещений и площадям этажей с картинки 470 px (размеры на ней не читаются); обмер и исходный проект — задание (К-1); высоты: 1-й этаж 2800 мм, мансарда 2700 мм (горизонтальная часть) приняты; скаты кровли мансарды приняты по картинке: колено 1200 мм, уклон 45°, конёк вдоль длинной стороны; проект КР — задание (К-2); наружные стены 400 мм, перегородки 120 мм приняты (К-1); разрешённая мощность 15 кВт принята по типовым ТУ для частного дома (К-4); подрайон климата не задан — принят не северный (жилые от 2,5 м) (К-7).

См. лист открытых вопросов (лист 8, записи К-1, К-2, К-4, К-7).

Примечания

1. Развёртки — вид на стену изнутри помещения, по часовой стрелке; расположение — на схеме листа и на листе 127; размеры — в мм по чистовым поверхностям; отметки — в м от ±0,000 (чистый пол 1-го этажа); высоты Н — от чистого пола помещения до оси изделия, у декора — до центра.
2. Красная цепочка — привязки электроточек и выводов по осям от угла чистовых стен; высота Н — у знака, от чистого пола до оси; высоты мебели, проёмов и границ отделки — колонкой отметок слева. Стена с 5 и более точками или с мелкими звеньями привязок показана двумя видами: архитектурная развёртка (мебель, отделка, проёмы, высоты) и вид «Привязки» на отдельном листе — точки и выводы с марками, одна цепочка по осям и таблица привязок (каждая точка — строка).
3. У знака электроточки: марка (Р — розетка, S — выключатель, Св — светильник, ЭВ — вывод кабеля), ×N — число постов в рамке, гр. — группа щита, Н — высота оси от чистого пола, мм; группы по клавишам выключателя — на листе выключателей.
4. Схема мебели, приборов и декора не является технической документацией для производства мебели; габариты — по паспортам изделий.

1000 мм · печать 1:1

Изм.	Кол.уч	Лист	№ док.	Подп.	Дата
Разраб.		Кырлан А.С.			04.11.26
Пров.					
ГИП					
Н. контр.					
Утв.					

ГД-2026-010-АИ

Дом 331 м²

Общая площадь 270,67* м² · * размеры приняты, не замерены (реестр — л. 8–10, К-1)

Дизайн-проект интерьера

Стадия	Лист	Листов
РП	157	216

Развёртки стен. Тамбур (пом. 9)

М 1:20

Кырлан Александр Сергеевич


выпуск 04.11.2026 № 2a77323a49 · стр. 161 из 221

Развёртка стены А. Гараж (пом. 10)

Гараж (пом. 10) · вид изнутри помещения · размеры в мм, отметки в м от ±0,000 (чистый пол 1-го этажа)


ПРЕДВАРИТЕЛЬНО · не для производства работ · открыто пунктов: 15 (реестр — л. 8–10)

Развёртка стены А

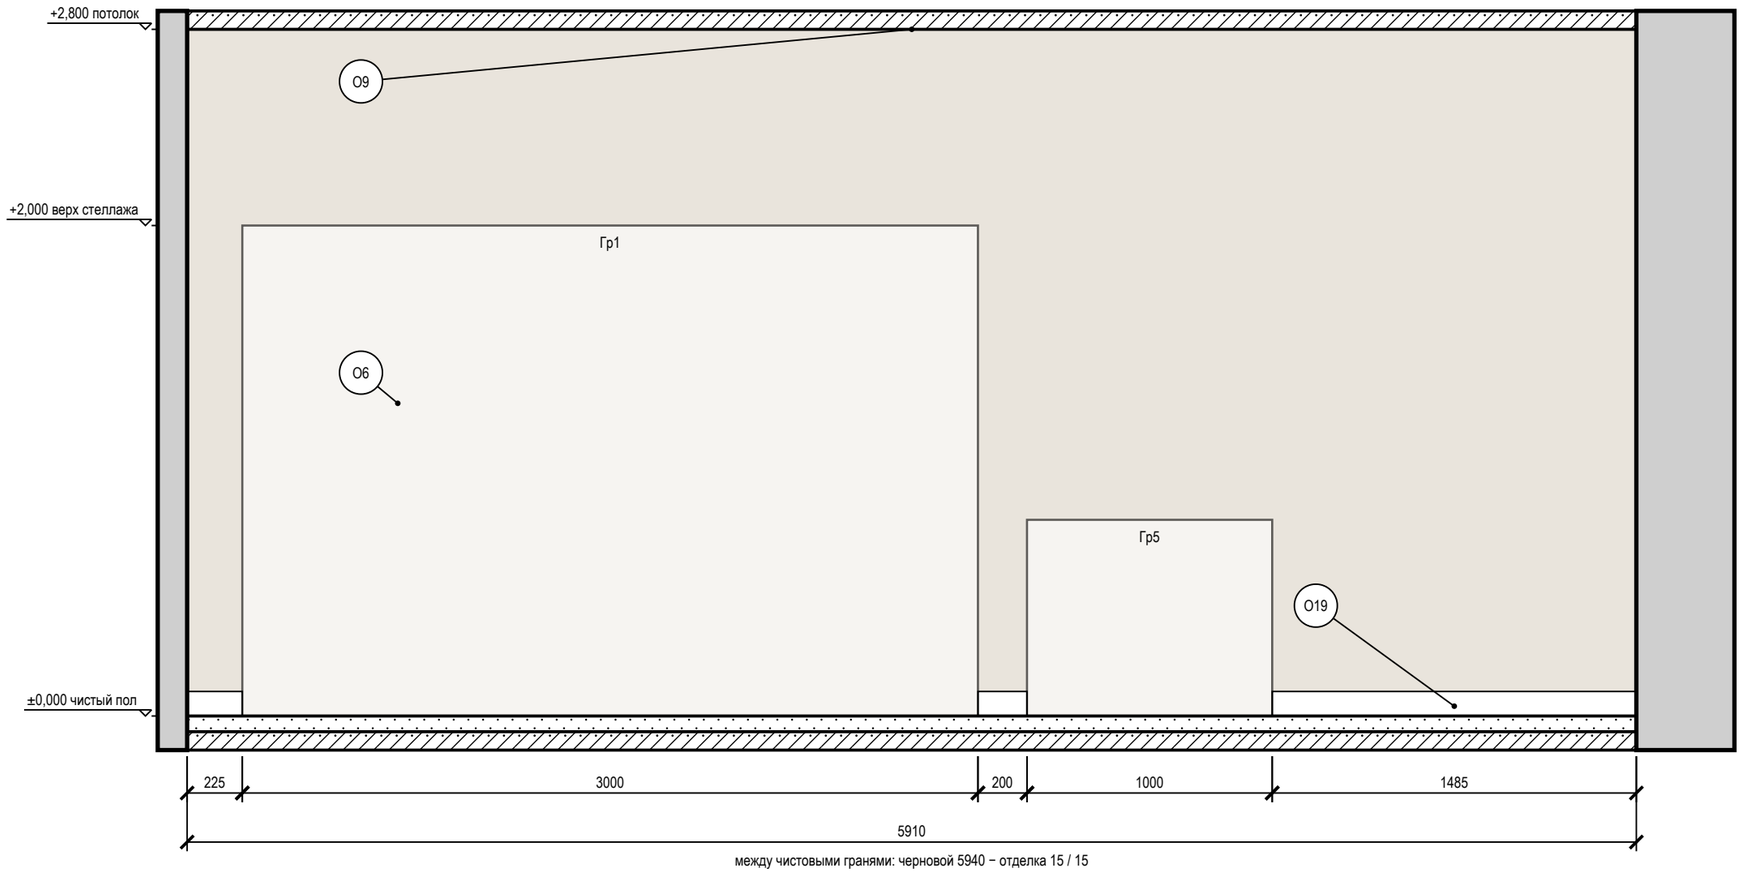

между чистовыми гранями: черновой 5940 − отделка 15 / 15

Схема развёрток (М 1:100)

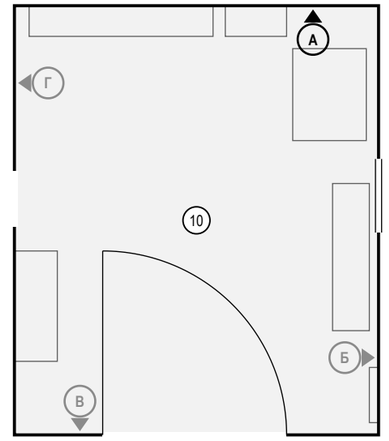

Условные обозначения

- мебель и приборы — фасад по расстановке (условно)
- стены и перекрытия в сечении
- окраска: тон — цвет по коду производителя (условно)
- О1 — марка отделки по реестру отделки альбома
- А — марка развёртки: буква стены, стрелка — взгляд

Ведомость отделки (на листе)

Марка	Поверхность	Материал, изделие	Цвет, код	Кол.
О6	стены	окраска, Farrow & Ball Modern Emulsion, матовая, подготовка Q3	Farrow & Ball No. 226 «Joa's White»	16,5 м²
О9	потолок	окраска, Little Greene Absolute Matt, глубокоматовая, подготовка Q3	Little Greene No. 105 «Slaked Lime»	41,6 м²
О19	плинтус	плинтус ПВХ, h 100 мм, аналог: плинтус ПВХ влагостойкий 100 мм, серый		1,9 м

Примечания

1. Развёртки — вид на стену изнутри помещения, по часовой стрелке; расположение — на схеме листа и на листе 127; размеры — в мм по чистовым поверхностям; отметки — в м от ±0,000 (чистый пол 1-го этажа); высоты Н — от чистого пола помещения до оси изделия, у декора — до центра.
2. Схема мебели, приборов и декора не является технической документацией для производства мебели; габариты — по паспортам изделий.

Допущения и предложения на листе

Основа листа: размеры и контуры этажей подобраны проектировщиком по составу помещений и площадям этажей с картинки 470 px (размеры на ней не читаются); обмер и исходный проект — задание (К-1); высоты: 1-й этаж 2800 мм, мансарда 2700 мм (горизонтальная часть) приняты; скаты кровли мансарды приняты по картинке: колено 1200 мм, уклон 45°, конёк вдоль длинной стороны; проект КР — задание (К-2); наружные стены 400 мм, перегородки 120 мм приняты (К-1); разрешённая мощность 15 кВт принята по типовым ТУ для частного дома (К-4); подрайон климата не задан — принят не северный (жилые от 2,5 м) (К-7).
См. лист открытых вопросов (лист 8, записи К-1, К-2, К-4, К-7).

1000 мм · печать 1:1

Изм.	Кол.уч	Лист	№ док.	Подп.	Дата
Разраб.		Кырлан А.С.			04.11.26
Пров.					
ГИП					
Н. контр.					
Утв.					

ГД-2026-010-АИ

Дом 331 м²

Общая площадь 270,67* м² · * размеры приняты, не замерены (реестр — л. 8–10, К-1)

Дизайн-проект интерьера	Стадия	Лист	Листов
	РП	158	216

Развёртка стены А. Гараж (пом. 10)

М 1:25


Кырлан Александр Сергеевич

выпуск 04.11.2026 № 2a77323a49 · стр. 162 из 221

Развёртка стены Б. Гараж (пом. 10)

Гараж (пом. 10) · вид изнутри помещения · размеры в мм, отметки в м от ±0,000 (чистый пол 1-го этажа)

Развёртка стены Б

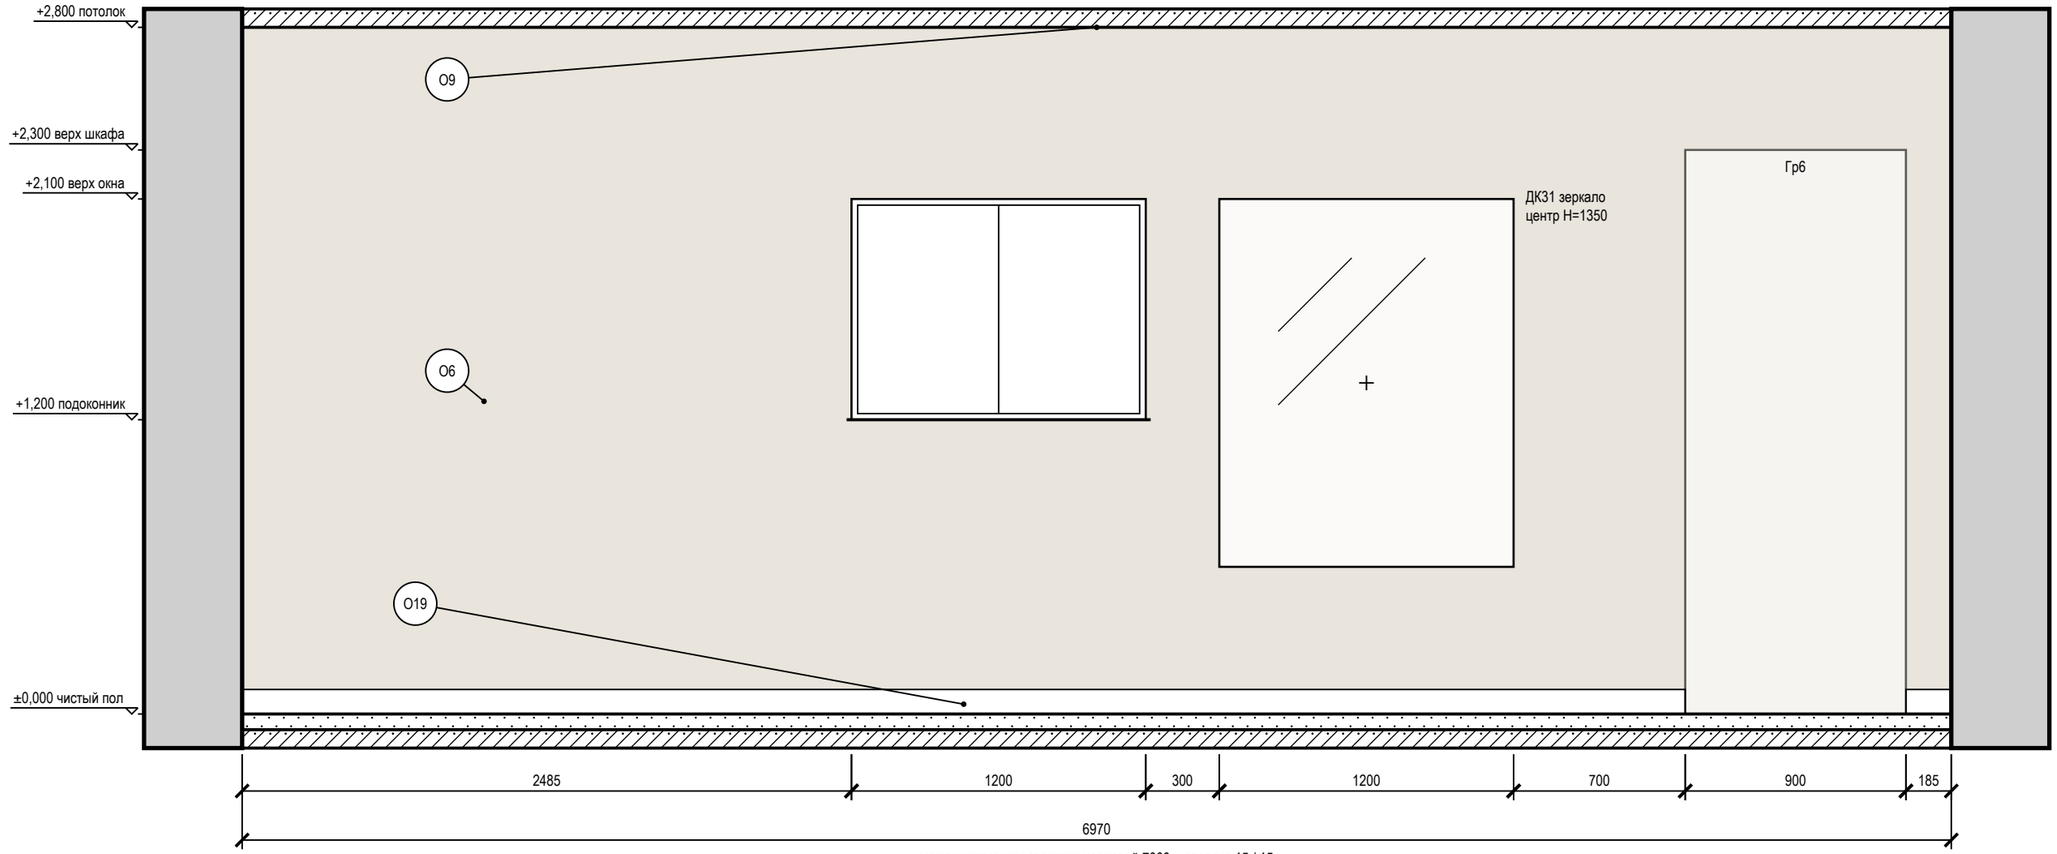

между чистовыми гранями: черновой 7000 − отделка 15 / 15

Условные обозначения

обозначения этого вида, схема развёрток помещения и ведомость отделки — на листе 160

Примечания

1. Развёртки — вид на стену изнутри помещения, по часовой стрелке; расположение — на схеме листа 160 и на листе 127; размеры — в мм по чистовым поверхностям; отметки — в м от ±0,000 (чистый пол 1-го этажа); высоты Н — от чистого пола помещения до оси изделия, у декора — до центра.
2. Схема мебели, приборов и декора не является технической документацией для производства мебели; габариты — по паспортам изделий.
3. Картины и зеркала крепить к основанию по паспорту изделия (закладные и анкеры — в перечне скрытых работ); крест — ось центра предмета.

Допущения и предложения на листе

Основа листа: размеры и контуры этажей подобраны проектировщиком по составу помещений и площадям этажей с картинки 470 px (размеры на ней не читаются); обмер и исходный проект — задание (К-1); высоты: 1-й этаж 2800 мм, мансарда 2700 мм (горизонтальная часть) приняты; скаты кровли мансарды приняты по картинке: колено 1200 мм, уклон 45°, конёк вдоль длинной стороны; проект КР — задание (К-2); наружные стены 400 мм, перегородки 120 мм приняты (К-1); разрешённая мощность 15 кВт принята по типовым ТУ для частного дома (К-4); подрайон климата не задан — принят не северный (жилые от 2,5 м) (К-7).
См. лист открытых вопросов (лист 8, записи К-1, К-2, К-4, К-7).

1000 мм · печать 1:1

Изм.	Кол.уч	Лист	№ док.	Подп.	Дата
Разраб.		Кырлан А.С.			04.11.26
Пров.					
ГИП					
Н. контр.					
Утв.					

ГД-2026-010-АИ

Дом 331 м²

Общая площадь 270,67* м² · * размеры приняты, не замерены (реестр — л. 8–10, К-1)

Дизайн-проект интерьера

Стадия	Лист	Листов
РП	159	216

Развёртка стены Б. Гараж (пом. 10)


М 1:25

Кырлан Александр Сергеевич

Развёртка стены Б: схема и ведомость отделки. Гараж (пом. 10)

Гараж (пом. 10) · к развёртке на листе 159

Схема развёрток (М 1:50)

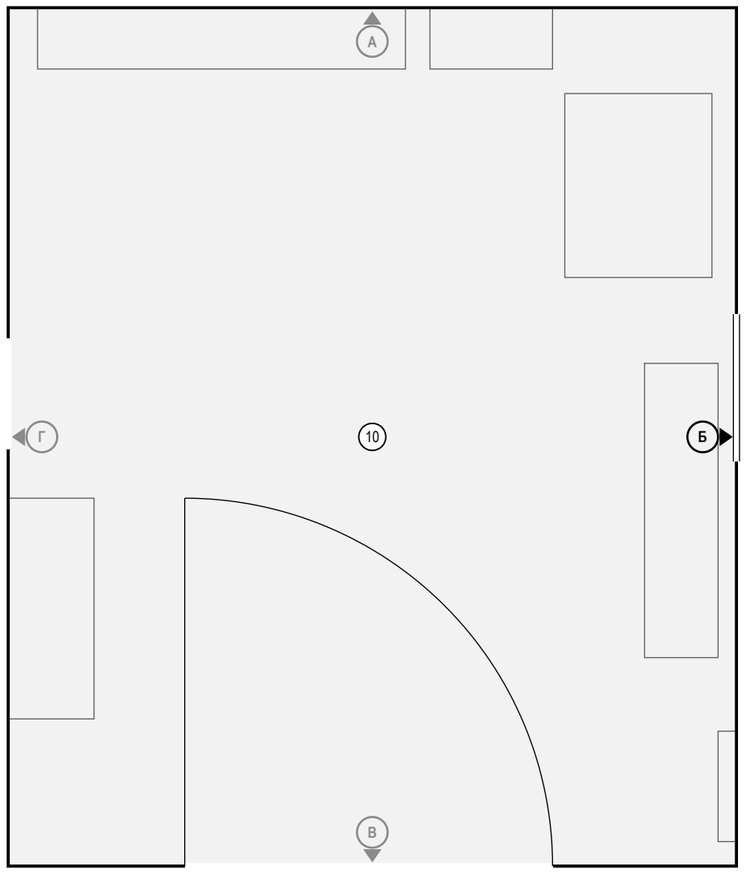

Условные обозначения

- мебель и приборы — фасад по расстановке (условно)
- зеркало: марка Д, крест — центр, Н — высота центра, мм
- окно: проём, рама, подоконник
- стены и перекрытия в сечении
- окраска: тон — цвет по коду производителя (условно)
- О1 — марка отделки по реестру отделки альбома
- А — марка развёртки: буква стены, стрелка — взгляд

Ведомость отделки (на листе)

Марка	Поверхность	Материал, изделие	Цвет, код	Кол.
О6	стены	окраска, Farrow & Ball Modern Emulsion, матовая, подготовка Q3	Farrow & Ball No. 226 «Joa's White»	18,4 м²
О9	потолок	окраска, Little Greene Absolute Matt, глубокоматовая, подготовка Q3	Little Greene No. 105 «Slaked Lime»	41,6 м²
О19	плинтус	плинтус ПВХ, h 100 мм, аналог: плинтус ПВХ влагостойкий 100 мм, серый		6,1 м

Примечания

1. Схема, условные обозначения и ведомость отделки — к развёртке стены Б на листе 159: вид в своём масштабе занимает лист целиком.
2. Расположение развёрток всех помещений — на листе 127; полная ведомость отделки — на листах отделочника.

Допущения и предложения на листе

Основа листа: размеры и контуры этажей подобраны проектировщиком по составу помещений и площадям этажей с картинки 470 px (размеры на ней не читаются); обмер и исходный проект — задание (К-1); высоты: 1-й этаж 2800 мм, мансарда 2700 мм (горизонтальная часть) приняты; скаты кровли мансарды приняты по картинке: колено 1200 мм, уклон 45°, конёк вдоль длинной стороны; проект КР — задание (К-2); наружные стены 400 мм, перегородки 120 мм приняты (К-1); разрешённая мощность 15 кВт принята по типовым ТУ для частного дома (К-4); подрайон климата не задан — принят не северный (жилые от 2,5 м) (К-7).

Знак «**» — предложение проектировщика, заказчиком не утверждено (согласовать с заказчиком): пол пом. 10 — покрытие пола гаража — предложение исполнителя: выдерживает шины, масло и антигололёдные реагенты, без швов; плинтус пом. 10 — артикул изделия не выбран: позиция описана характеристиками («аналог по характеристикам»), артикул выбирается при закупке.

См. лист открытых вопросов (лист 8, записи К-1, К-2, К-4, К-7).

Изм.	Кол.уч	Лист	№ док.	Подп.	Дата
Разраб.		Кырлан А.С.			04.11.26
Пров.					
ГИП					
Н. контр.					
Утв.					

ГД-2026-010-АИ

Дом 331 м²

Общая площадь 270,67* м² · * размеры приняты, не замерены (реестр — л. 8–10, К-1)

Дизайн-проект интерьера

Стадия	Лист	Листов
РП	160	216

Развёртка стены Б: схема и ведомость отделки. Гараж (пом. 10)

М б/м


Кырлан Александр Сергеевич

Развёртка стены В. Гараж (пом. 10)

Гараж (пом. 10) · вид изнутри помещения · размеры в мм, отметки в м от ±0,000 (чистый пол 1-го этажа)


ПРЕДВАРИТЕЛЬНО · не для производства работ · открыто пунктов: 15 (реестр — л. 8–10)

Развёртка стены В

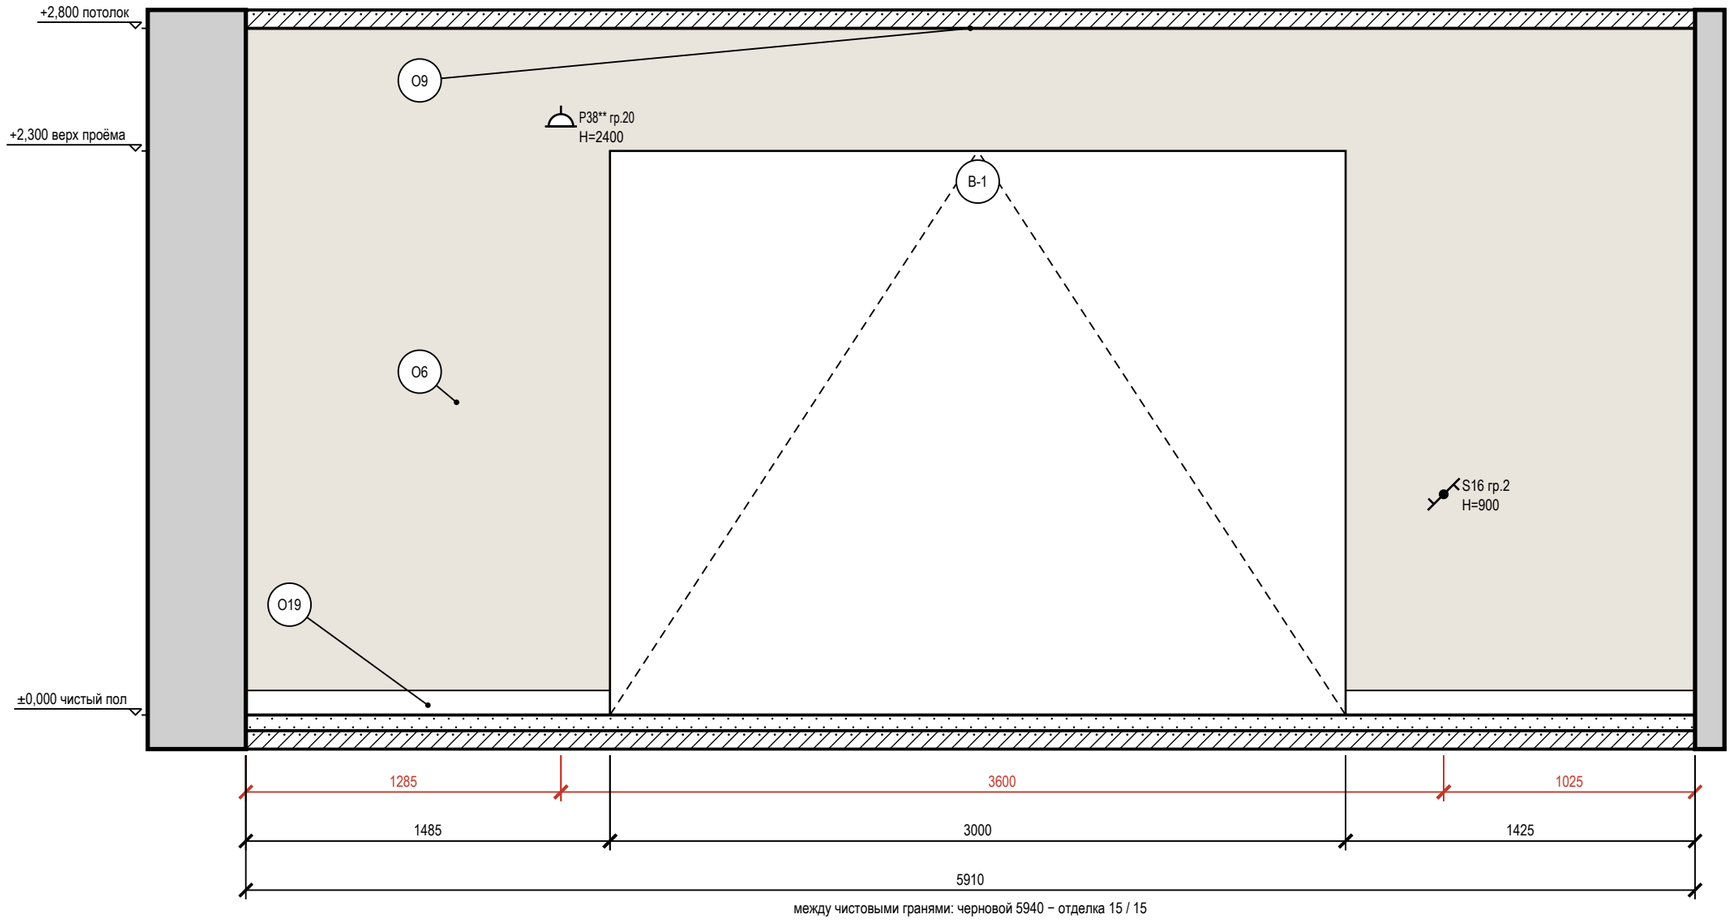

между чистовыми гранями: черновой 5940 − отделка 15 / 15

Схема развёрток (М 1:100)

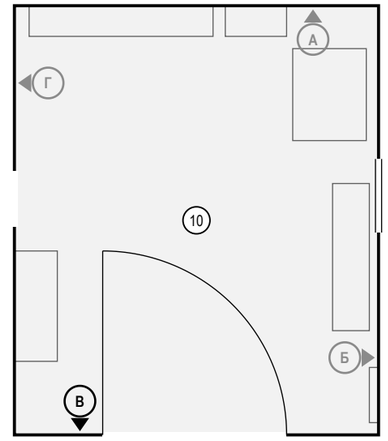

Условные обозначения

- розетка с заземляющим контактом; у знака — марка, ×N постов в рамке, гр. — группа щита, H — высота оси, мм
- выключатель одноклавишный
- выключатель с проходной или перекрёстной клавишей (обратный флажок); тип клавиши — в подписи
- привязки точек и выводов от угла и от пола, мм
- мебель и приборы — фасад по расстановке (условно)
- дверной проём; марка двери — в кружке
- стены и перекрытия в сечении
- окраска: тон — цвет по коду производителя (условно)
- О1 — марка отделки по реестру отделки альбома
- А — марка развёртки: буква стены, стрелка — взгляд

Ведомость отделки (на листе)

Марка	Поверхность	Материал, изделие	Цвет, код	Кол.
О6	стены	окраска, Farrow & Ball Modern Emulsion, матовая, подготовка Q3	Farrow & Ball No. 226 «Joa's White»	9,6 м²
О9	потолок	окраска, Little Greene Absolute Matt, глубокоматовая, подготовка Q3	Little Greene No. 105 «Slaked Lime»	41,6 м²
О19	плинтус	плинтус ПВХ, h 100 мм, аналог: плинтус ПВХ влагостойкий 100 мм, серый		2,9 м

Допущения и предложения на листе

Основа листа: размеры и контуры этажей подобраны проектировщиком по составу помещений и площадям этажей с картинки 470 px (размеры на ней не читаются); обмер и исходный проект — задание (К-1); высоты: 1-й этаж 2800 мм, мансарда 2700 мм (горизонтальная часть) приняты; скаты кровли мансарды приняты по картинке: колено 1200 мм, уклон 45°, конёк вдоль длинной стороны; проект КР — задание (К-2); наружные стены 400 мм, перегородки 120 мм приняты (К-1); разрешённая мощность 15 кВт принята по типовым ТУ для частного дома (К-4); подрайон климата не задан — принят не северный (жилые от 2,5 м) (К-7).

Знак «**» — предложение проектировщика, заказчиком не утверждено (согласовать с заказчиком): Р38 — высота 2400 мм выше 1 м по назначению: питание привода ворот у его места на потолке.

См. лист открытых вопросов (лист 8, записи К-1, К-2, К-4, К-7).

Примечания

1. Развёртки — вид на стену изнутри помещения, по часовой стрелке; расположение — на схеме листа и на листе 127; размеры — в мм по чистовым поверхностям; отметки — в м от ±0,000 (чистый пол 1-го этажа); высоты H — от чистого пола помещения до оси изделия, у декора — до центра.
2. Красная цепочка — привязки электроточек и выводов по осям от угла чистовых стен; высота H — у знака, от чистого пола до оси; высоты мебели, проёмов и границ отделки — колонкой отметок слева. Стена с 5 и более точками или с мелкими звеньями привязок показана двумя видами: архитектурная развёртка (мебель, отделка, проёмы, высоты) и вид «Привязки» на отдельном листе — точки и выводы с марками, одна цепочка по осям и таблица привязок (каждая точка — строка).
3. У знака электроточки: марка (Р — розетка, S — выключатель, Св — светильник, ЭВ — вывод кабеля), ×N — число постов в рамке, гр. — группа щита, H — высота оси от чистого пола, мм; группы по клавишам выключателя — на листе выключателей.
4. Схема мебели, приборов и декора не является технической документацией для производства мебели; габариты — по паспортам изделий.

1000 мм · печать 1:1

Изм.	Кол.уч	Лист	№ док.	Подп.	Дата
Разраб.		Кырлан А.С.			04.11.26
Пров.					
ГИП					
Н. контр.					
Утв.					

ГД-2026-010-АИ

Дом 331 м²

Общая площадь 270,67* м² · * размеры приняты, не замерены (реестр — л. 8–10, К-1)

Дизайн-проект интерьера

Стадия	Лист	Листов
РП	161	216

Развёртка стены В. Гараж (пом. 10)

М 1:25


Кырлан Александр Сергеевич

Развёртка стены Г. Гараж (пом. 10)

Гараж (пом. 10) · вид изнутри помещения · размеры в мм, отметки в м от ±0,000 (чистый пол 1-го этажа)

ПРЕДВАРИТЕЛЬНО · не для производства работ · открыто пунктов: 15 (реестр — л. 8–10)

Развёртка стены Г

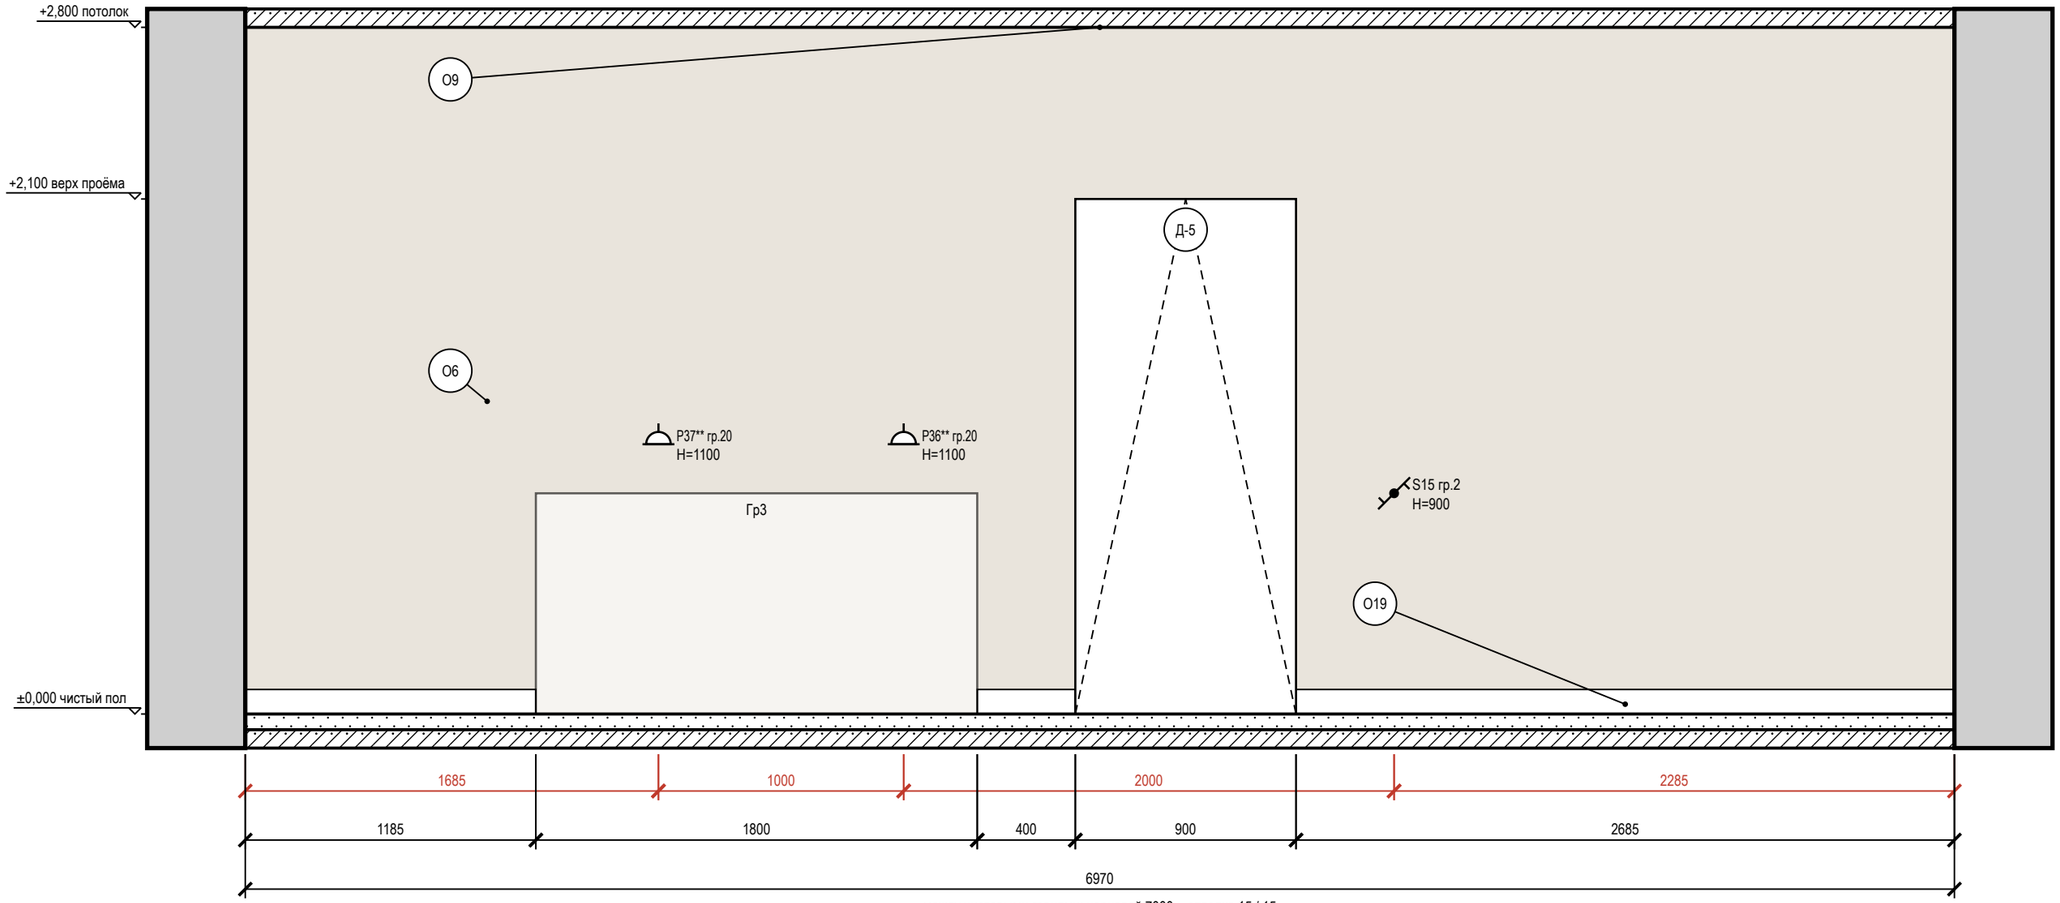

между чистовыми гранями: черновой 7000 − отделка 15 / 15

Условные обозначения

обозначения этого вида, схема развёрток помещения и ведомость отделки — на листе 163

Допущения и предложения на листе

Основа листа: размеры и контуры этажей подобраны проектировщиком по составу помещений и площадям этажей с картинки 470 px (размеры на ней не читаются); обмер и исходный проект — задание (К-1); высоты: 1-й этаж 2800 мм, мансарда 2700 мм (горизонтальная часть) приняты; скаты кровли мансарды приняты по картинке: колено 1200 мм, уклон 45°, конёк вдоль длинной стороны; проект КР — задание (К-2); наружные стены 400 мм, перегородки 120 мм приняты (К-1); разрешённая мощность 15 кВт принята по типовым ТУ для частного дома (К-4); подрайон климата не задан — принят не северный (жилые от 2,5 м) (К-7).

Знак «**» — предложение проектировщика, заказчиком не утверждено (согласовать с заказчиком): Р36, Р37 — высота 1100 мм выше 1 м по назначению: над столешницей верстака 900 мм.

См. лист открытых вопросов (лист 8, записи К-1, К-2, К-4, К-7).

Примечания

1. Развёртки — вид на стену изнутри помещения, по часовой стрелке; расположение — на схеме листа 163 и на листе 127; размеры — в мм по чистовым поверхностям; отметки — в м от ±0,000 (чистый пол 1-го этажа); высоты H — от чистого пола помещения до оси изделия, у декора — до центра.
2. Красная цепочка — привязки электроточек и выводов по осям от угла чистовых стен; высота H — у знака, от чистого пола до оси; высоты мебели, проёмов и границ отделки — колонкой отметок слева. Стена с 5 и более точками или с мелкими звеньями привязок показана двумя видами: архитектурная развёртка (мебель, отделка, проёмы, высоты) и вид «Привязки» на отдельном листе — точки и выводы с марками, одна цепочка по осям и таблица привязок (каждая точка — строка).
3. У знака электроточки: марка (Р — розетка, S — выключатель, Св — светильник, ЭВ — вывод кабеля), ×N — число постов в рамке, гр. — группа щита, H — высота оси от чистого пола, мм; группы по клавишам выключателя — на листе выключателей.
4. Схема мебели, приборов и декора не является технической документацией для производства мебели; габариты — по паспортам изделий.

1000 мм · печать 1:1

Изм.	Кол.уч	Лист	№ док.	Подп.	Дата
Разраб.		Кырлан А.С.			04.11.26
Пров.					
ГИП					
Н. контр.					
Утв.					

ГД-2026-010-АИ

Дом 331 м²

Общая площадь 270,67* м² · * размеры приняты, не замерены (реестр — л. 8–10, К-1)

Дизайн-проект интерьера

Стадия	Лист	Листов
РП	162	216

Развёртка стены Г. Гараж (пом. 10)

М 1:25


Кырлан Александр Сергеевич

выпуск 04.11.2026 № 2a77323a49 · стр. 166 из 221

Развёртка стены Г: схема и ведомость отделки. Гараж (пом. 10)

Гараж (пом. 10) · к развёртке на листе 162

Схема развёрток (М 1:50)

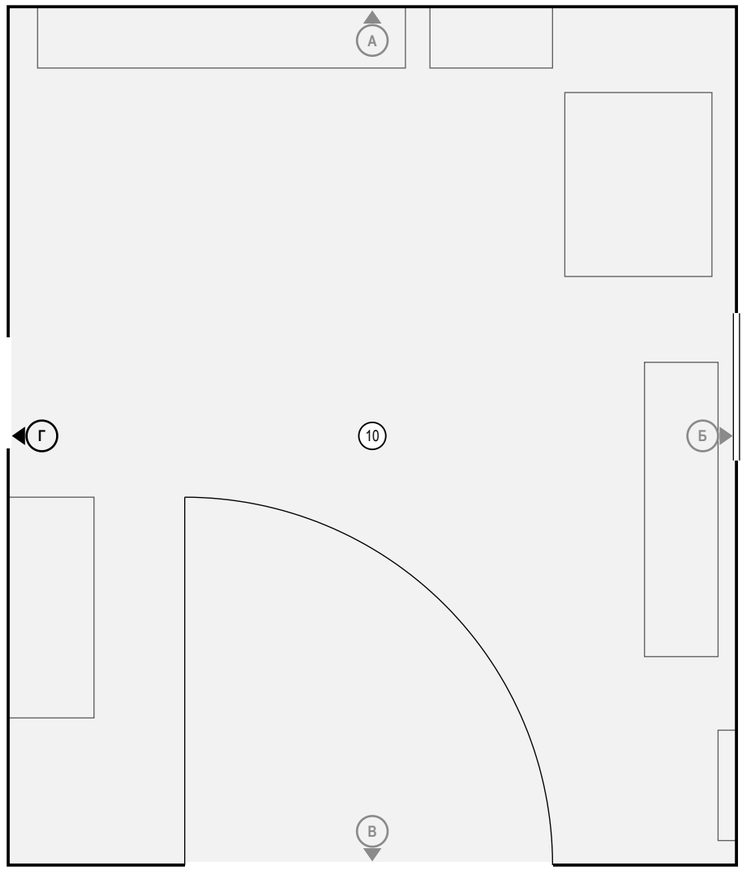

Условные обозначения

- розетка с заземляющим контактом; у знака — марка, ×N постов в рамке, гр. — группа щита, Н — высота оси, мм
- выключатель одноклавишный
- выключатель с проходной или перекрёстной клавишей (обратный флажок); тип клавиши — в подписи
- привязки точек и выводов от угла и от пола, мм
- мебель и приборы — фасад по расстановке (условно)
- дверной проём; марка двери — в кружке
- стены и перекрытия в сечении
- окраска: тон — цвет по коду производителя (условно)
- О1 — марка отделки по реестру отделки альбома
- А — марка развёртки: буква стены, стрелка — взгляд

Ведомость отделки (на листе)

Марка	Поверхность	Материал, изделие	Цвет, код	Кол.
О6	стены	окраска, Farrow & Ball Modern Emulsion, матовая, подготовка Q3	Farrow & Ball No. 226 «Joa's White»	17,6 м²
О9	потолок	окраска, Little Greene Absolute Matt, глубокоматовая, подготовка Q3	Little Greene No. 105 «Slaked Lime»	41,6 м²
О19	плинтус	плинтус ПВХ, h 100 мм, аналог: плинтус ПВХ влагостойкий 100 мм, серый		4,3 м

Примечания

1. Схема, условные обозначения и ведомость отделки — к развёртке стены Г на листе 162: вид в своём масштабе занимает лист целиком.
2. Расположение развёрток всех помещений — на листе 127; полная ведомость отделки — на листах отделочника.

Допущения и предложения на листе

Основа листа: размеры и контуры этажей подобраны проектировщиком по составу помещений и площадям этажей с картинки 470 px (размеры на ней не читаются); обмер и исходный проект — задание (К-1); высоты: 1-й этаж 2800 мм, мансарда 2700 мм (горизонтальная часть) приняты; скаты кровли мансарды приняты по картинке: колено 1200 мм, уклон 45°, конёк вдоль длинной стороны; проект КР — задание (К-2); наружные стены 400 мм, перегородки 120 мм приняты (К-1); разрешённая мощность 15 кВт принята по типовым ТУ для частного дома (К-4); подрайон климата не задан — принят не северный (жилые от 2,5 м) (К-7).

Знак «**» — предложение проектировщика, заказчиком не утверждено (согласовать с заказчиком): пол пом. 10 — покрытие пола гаража — предложение исполнителя: выдерживает шины, масло и антигололёдные реагенты, без швов; плинтус пом. 10 — артикул изделия не выбран: позиция описана характеристиками («аналог по характеристикам»), артикул выбирается при закупке.

См. лист открытых вопросов (лист 8, записи К-1, К-2, К-4, К-7).

Изм.	Кол.уч	Лист	№ док.	Подп.	Дата
Разраб.		Кырлан А.С.			04.11.26
Пров.					
ГИП					
Н. контр.					
Утв.					

ГД-2026-010-АИ

Дом 331 м²

Общая площадь 270,67* м² · * размеры приняты, не замерены (реестр — л. 8–10, К-1)

Дизайн-проект интерьера

Стадия	Лист	Листов
РП	163	216

Развёртка стены Г: схема и ведомость отделки. Гараж (пом. 10)

М б/м

Кырлан Александр Сергеевич

Развёртка стены А. Веранда (пом. 11)

Веранда (пом. 11) · вид изнутри помещения · размеры в мм, отметки в м от ±0,000 (чистый пол 1-го этажа)

ПРЕДВАРИТЕЛЬНО · не для производства работ · открыто пунктов: 15 (реестр — л. 8–10)

Развёртка стены А


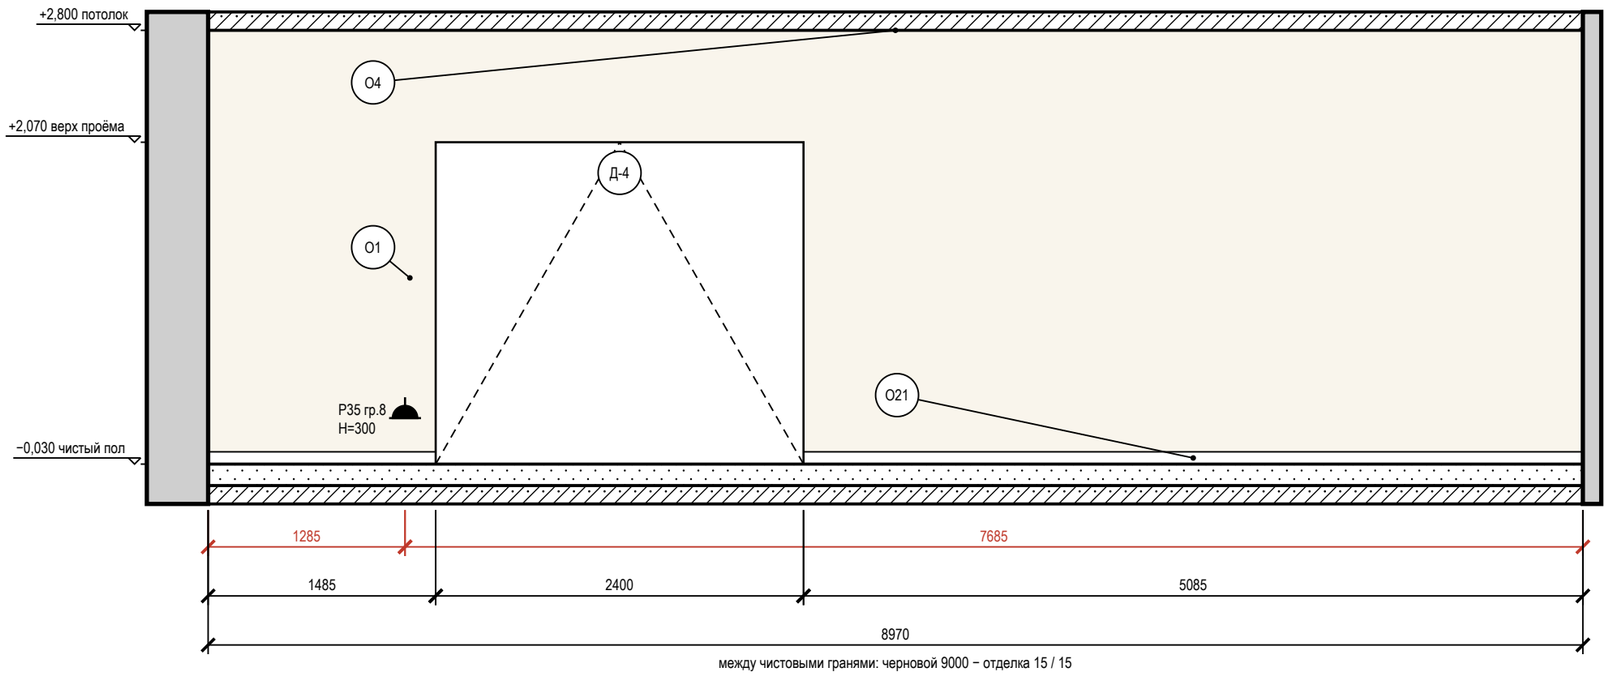


Схема развёрток (М 1:100)

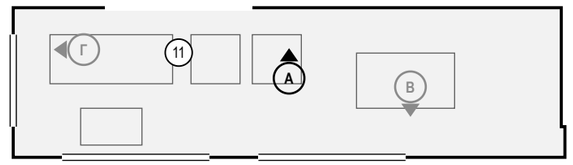

Условные обозначения

- розетка влагозащищённая IP44
- привязки точек и выводов от угла и от пола, мм
- мебель и приборы — фасад по расстановке (условно)
- дверной проём; марка двери — в кружке
- стены и перекрытия в сечении
- окраска: тон — цвет по коду производителя (условно)
- О1 — марка отделки по реестру отделки альбома
- А — марка развёртки: буква стены, стрелка — взгляд

Ведомость отделки (на листе)

Марка	Поверхность	Материал, изделие	Цвет, код	Кол.
О1	стены	окраска, Tikkurila Luja 7, шелковисто-матовая, подготовка К3	NCS S 0804-Y30R «S 0804-Y30R»	20,3 м²
О4	потолок	окраска, Tikkurila Luja 7, матовая, подготовка Q3	NCS S 0804-Y30R «S 0804-Y30R»	21,8 м²
О21	плинтус	керамогранит, аналог: плинтус из керамогранита пола, подрезка 80 мм, верхняя кромка с запилом 45°	#B8AFA5 «тон Claystone V486»	6,6 м

Допущения и предложения на листе

Основа листа: размеры и контуры этажей подобраны проектировщиком по составу помещений и площадям этажей с картинки 470 px (размеры на ней не читаются); обмер и исходный проект — задание (К-1); высоты: 1-й этаж 2800 мм, мансарда 2700 мм (горизонтальная часть) приняты; скаты кровли мансарды приняты по картинке: колено 1200 мм, уклон 45°, конёк вдоль длинной стороны; проект КР — задание (К-2); наружные стены 400 мм, перегородки 120 мм приняты (К-1); разрешённая мощность 15 кВт принята по типовым ТУ для частного дома (К-4); подрайон климата не задан — принят не северный (жилые от 2,5 м) (К-7).

См. лист открытых вопросов (лист 8, записи К-1, К-2, К-4, К-7).

Примечания

1. Развёртки — вид на стену изнутри помещения, по часовой стрелке; расположение — на схеме листа и на листе 127; размеры — в мм по чистовым поверхностям; отметки — в м от ±0,000 (чистый пол 1-го этажа); высоты Н — от чистого пола помещения до оси изделия, у декора — до центра.
2. Красная цепочка — привязки электроточек и выводов по осям от угла чистовых стен; высота Н — у знака, от чистого пола до оси; высоты мебели, проёмов и границ отделки — колонкой отметок слева. Стена с 5 и более точками или с мелкими звеньями привязок показана двумя видами: архитектурная развёртка (мебель, отделка, проёмы, высоты) и вид «Привязки» на отдельном листе — точки и выводы с марками, одна цепочка по осям и таблица привязок (каждая точка — строка).
3. У знака электроточки: марка (Р — розетка, S — выключатель, Св — светильник, ЭВ — вывод кабеля), ×N — число постов в рамке, гр. — группа щита, Н — высота оси от чистого пола, мм; группы по клавишам выключателя — на листе выключателей.
4. Схема мебели, приборов и декора не является технической документацией для производства мебели; габариты — по паспортам изделий.

1000 мм · печать 1:1

Изм.	Кол.уч	Лист	№ док.	Подп.	Дата
Разраб.		Кырлан А.С.			04.11.26
Пров.					
ГИП					
Н. контр.					
Утв.					

ГД-2026-010-АИ

Дом 331 м²

Общая площадь 270,67* м² · * размеры приняты, не замерены (реестр — л. 8–10, К-1)

Дизайн-проект интерьера

Стадия	Лист	Листов
РП	164	216

Развёртка стены А. Веранда (пом. 11)

М 1:40

Кырлан Александр Сергеевич

выпуск 04.11.2026 № 2a77323a49 · стр. 168 из 221

Развёртка стены В. Веранда (пом. 11)

Веранда (пом. 11) · вид изнутри помещения · размеры в мм, отметки в м от ±0,000 (чистый пол 1-го этажа)

Развёртка стены В


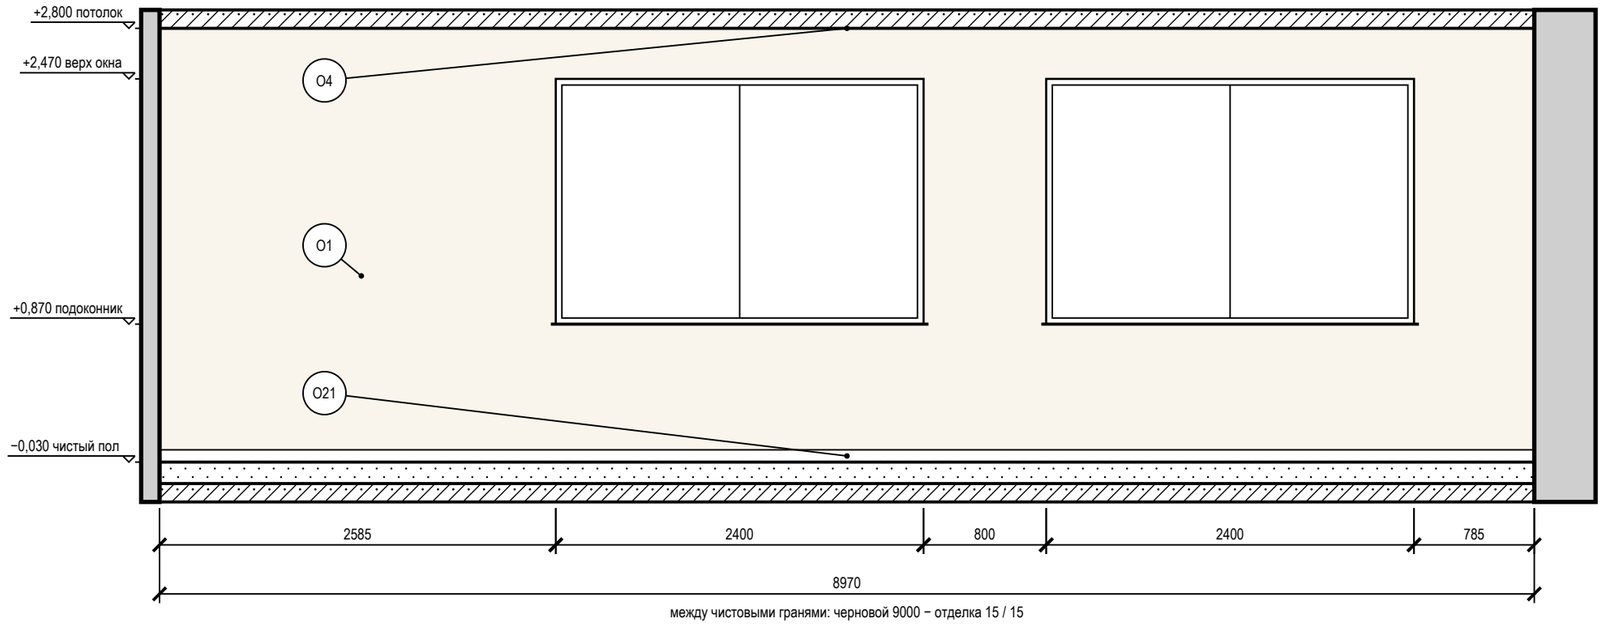


Схема развёрток (М 1:100)

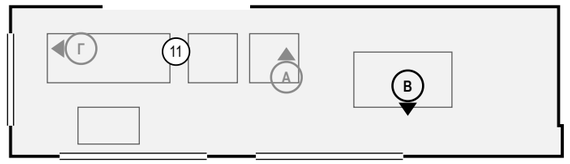

Условные обозначения

- мебель и приборы — фасад по расстановке (условно)
- окно: проём, рама, подоконник
- стены и перекрытия в сечении
- окраска: тон — цвет по коду производителя (условно)
- О1 — марка отделки по реестру отделки альбома
- А — марка развёртки: буква стены, стрелка — взгляд

Ведомость отделки (на листе)

Марка	Поверхность	Материал, изделие	Цвет, код	Кол.
О1	стены	окраска, Tikkurila Luja 7, шелковисто-матовая, подготовка К3	NCS S 0804-Y30R «S 0804-Y30R»	17,7 м²
О4	потолок	окраска, Tikkurila Luja 7, матовая, подготовка Q3	NCS S 0804-Y30R «S 0804-Y30R»	21,8 м²
О21	плинтус	керамогранит, аналог: плинтус из керамогранита пола, подрезка 80 мм, верхняя кромка с запилом 45°	#B8AFA5 «тон Claystone V486»	9 м

Примечания

1. Развёртки — вид на стену изнутри помещения, по часовой стрелке; расположение — на схеме листа и на листе 127; размеры — в мм по чистовым поверхностям; отметки — в м от ±0,000 (чистый пол 1-го этажа); высоты Н — от чистого пола помещения до оси изделия, у декора — до центра.
2. Схема мебели, приборов и декора не является технической документацией для производства мебели; габариты — по паспортам изделий.

Допущения и предложения на листе

Основа листа: размеры и контуры этажей подобраны проектировщиком по составу помещений и площадям этажей с картинки 470 px (размеры на ней не читаются); обмер и исходный проект — задание (К-1); высоты: 1-й этаж 2800 мм, мансарда 2700 мм (горизонтальная часть) приняты; скаты кровли мансарды приняты по картинке: колено 1200 мм, уклон 45°, конёк вдоль длинной стороны; проект КР — задание (К-2); наружные стены 400 мм, перегородки 120 мм приняты (К-1); разрешённая мощность 15 кВт принята по типовым ТУ для частного дома (К-4); подрайон климата не задан — принят не северный (жилые от 2,5 м) (К-7).
См. лист открытых вопросов (лист 8, записи К-1, К-2, К-4, К-7).

1000 мм · печать 1:1

Изм.	Кол.уч	Лист	№ док.	Подп.	Дата
Разраб.		Кырлан А.С.			04.11.26
Пров.					
ГИП					
Н. контр.					
Утв.					

ГД-2026-010-АИ

Дом 331 м²

Общая площадь 270,67* м² · * размеры приняты, не замерены (реестр — л. 8–10, К-1)

Дизайн-проект интерьера

Стадия	Лист	Листов
РП	165	216

Развёртка стены В. Веранда (пом. 11)

М 1:40


Кырлан Александр Сергеевич

Развёртка стены Г. Веранда (пом. 11)

Веранда (пом. 11) · вид изнутри помещения · размеры в мм, отметки в м от ±0,000 (чистый пол 1-го этажа)


ПРЕДВАРИТЕЛЬНО · не для производства работ · открыто пунктов: 15 (реестр — л. 8–10)

Развёртка стены Г

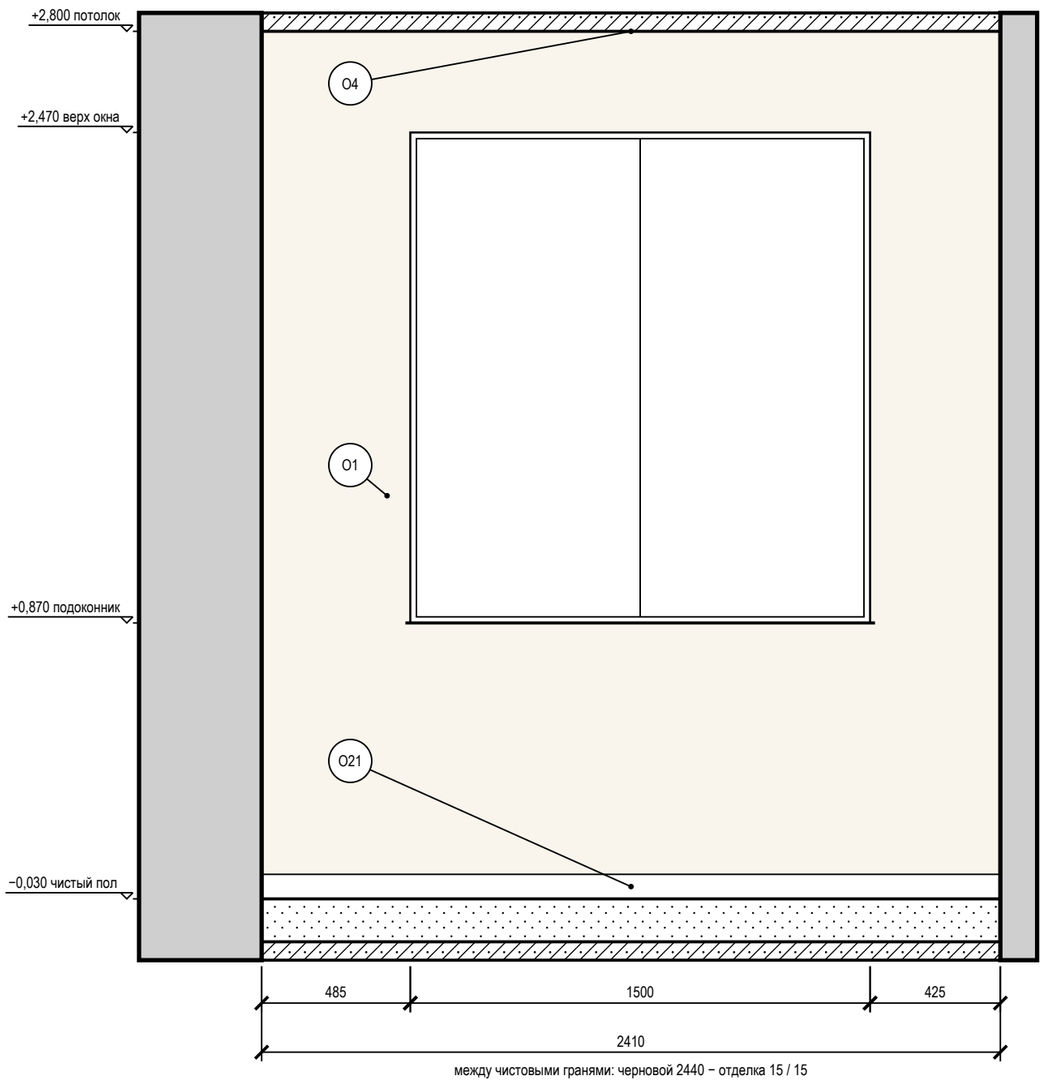

между чистовыми гранями: черновой 2440 − отделка 15 / 15

Схема развёрток (М 1:100)

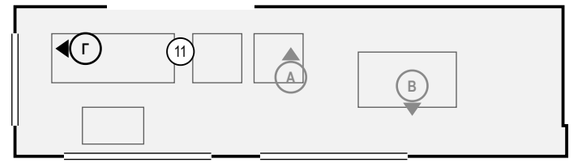

Условные обозначения

- мебель и приборы — фасад по расстановке (условно)
- окно: проём, рама, подоконник
- стены и перекрытия в сечении
- окраска: тон — цвет по коду производителя (условно)
- О1 — марка отделки по реестру отделки альбома
- А — марка развёртки: буква стены, стрелка — взгляд

Ведомость отделки (на листе)

Марка	Поверхность	Материал, изделие	Цвет, код	Кол.
О1	стены	окраска, Tikkurila Luja 7, шелковисто-матовая, подготовка К3	NCS S 0804-Y30R «S 0804-Y30R»	4,4 м²
О4	потолок	окраска, Tikkurila Luja 7, матовая, подготовка Q3	NCS S 0804-Y30R «S 0804-Y30R»	21,8 м²
О21	плинтус	керамогранит, аналог: плинтус из керамогранита пола, подрезка 80 мм, верхняя кромка с запилом 45°	#B8AFA5 «тон Claystone V486»	2,4 м

Примечания

1. Развёртки — вид на стену изнутри помещения, по часовой стрелке; расположение — на схеме листа и на листе 127; размеры — в мм по чистовым поверхностям; отметки — в м от ±0,000 (чистый пол 1-го этажа); высоты Н — от чистого пола помещения до оси изделия, у декора — до центра.
2. Схема мебели, приборов и декора не является технической документацией для производства мебели; габариты — по паспортам изделий.

Допущения и предложения на листе

Основа листа: размеры и контуры этажей подобраны проектировщиком по составу помещений и площадям этажей с картинки 470 px (размеры на ней не читаются); обмер и исходный проект — задание (К-1); высоты: 1-й этаж 2800 мм, мансарда 2700 мм (горизонтальная часть) приняты; скаты кровли мансарды приняты по картинке: колено 1200 мм, уклон 45°, конёк вдоль длинной стороны; проект КР — задание (К-2); наружные стены 400 мм, перегородки 120 мм приняты (К-1); разрешённая мощность 15 кВт принята по типовым ТУ для частного дома (К-4); подрайон климата не задан — принят не северный (жилые от 2,5 м) (К-7).
См. лист открытых вопросов (лист 8, записи К-1, К-2, К-4, К-7).

1000 мм · печать 1:1

Изм.	Кол.уч	Лист	№ док.	Подп.	Дата
Разраб.		Кырлан А.С.			04.11.26
Пров.					
ГИП					
Н. контр.					
Утв.					

ГД-2026-010-АИ

Дом 331 м²

Общая площадь 270,67* м² · * размеры приняты, не замерены (реестр — л. 8–10, К-1)

Дизайн-проект интерьера	Стадия	Лист	Листов
	РП	166	216

Развёртка стены Г. Веранда (пом. 11)

М 1:20


Кырлан Александр Сергеевич

выпуск 04.11.2026 № 2a77323a49 · стр. 170 из 221

Развёртки стен. Крыльцо (пом. 12)


Крыльцо (пом. 12) · вид изнутри помещения · размеры в мм, отметки в м от ±0,000 (чистый пол 1-го этажа)

Развёртка стены А

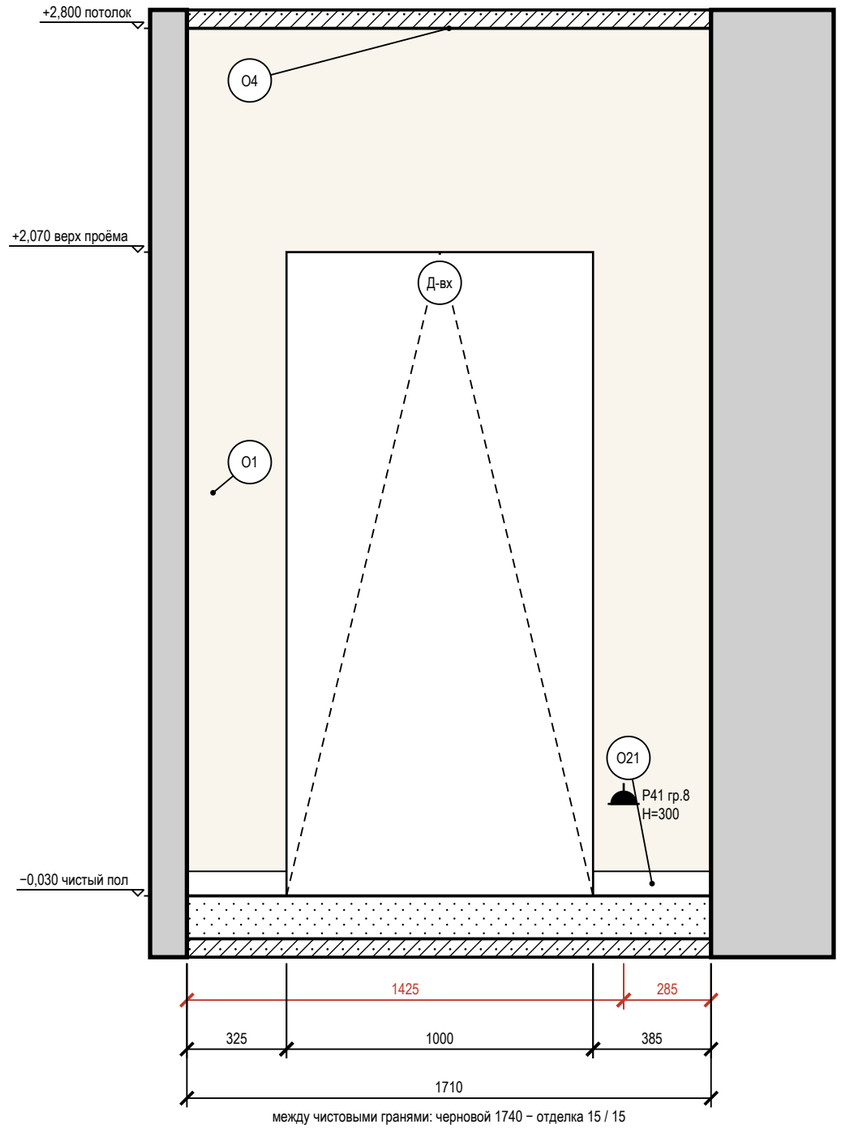

между чистовыми гранями: черновой 1740 − отделка 15 / 15

Схема развёрток (М 1:100)

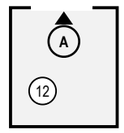

Условные обозначения

- розетка влагозащищённая IP44
- привязки точек и выводов от угла и от пола, мм
- мебель и приборы — фасад по расстановке (условно)
- дверной проём; марка двери — в кружке
- стены и перекрытия в сечении
- окраска: тон — цвет по коду производителя (условно)
- О1 — марка отделки по реестру отделки альбома
- A — марка развёртки: буква стены, стрелка — взгляд

Ведомость отделки (на листе)

Марка	Поверхность	Материал, изделие	Цвет, код	Кол.
О1	стены	окраска, Tikkurila Luja 7, шелковисто-матовая, подготовка К3	NCS S 0804-Y30R «S 0804-Y30R»	2,7 м²
О4	потолок	окраска, Tikkurila Luja 7, матовая, подготовка Q3	NCS S 0804-Y30R «S 0804-Y30R»	3,4 м²
О21	плинтус	керамогранит, аналог: плинтус из керамогранита пола, подрезка 80 мм, верхняя кромка с запилом 45°	#B8AFA5 «тон Claystone V486»	0,7 м

Допущения и предложения на листе

Основа листа: размеры и контуры этажей подобраны проектировщиком по составу помещений и площадям этажей с картинки 470 px (размеры на ней не читаются); обмер и исходный проект — задание (К-1); высоты: 1-й этаж 2800 мм, мансарда 2700 мм (горизонтальная часть) приняты; скаты кровли мансарды приняты по картинке: колено 1200 мм, уклон 45°, конёк вдоль длинной стороны; проект КР — задание (К-2); наружные стены 400 мм, перегородки 120 мм приняты (К-1); разрешённая мощность 15 кВт принята по типовым ТУ для частного дома (К-4); подрайон климата не задан — принят не северный (жилые от 2,5 м) (К-7).

См. лист открытых вопросов (лист 8, записи К-1, К-2, К-4, К-7).

Примечания

1. Развёртки — вид на стену изнутри помещения, по часовой стрелке; расположение — на схеме листа и на листе 127; размеры — в мм по чистовым поверхностям; отметки — в м от ±0,000 (чистый пол 1-го этажа); высоты Н — от чистого пола помещения до оси изделия, у декора — до центра.
2. Красная цепочка — привязки электроточек и выводов по осям от угла чистовых стен; высота Н — у знака, от чистого пола до оси; высоты мебели, проёмов и границ отделки — колонкой отметок слева. Стена с 5 и более точками или с мелкими звеньями привязок показана двумя видами: архитектурная развёртка (мебель, отделка, проёмы, высоты) и вид «Привязки» на отдельном листе — точки и выводы с марками, одна цепочка по осям и таблица привязок (каждая точка — строка).
3. У знака электроточки: марка (Р — розетка, S — выключатель, Св — светильник, ЭВ — вывод кабеля), ×N — число постов в рамке, гр. — группа щита, Н — высота оси от чистого пола, мм; группы по клавишам выключателя — на листе выключателей.
4. Схема мебели, приборов и декора не является технической документацией для производства мебели; габариты — по паспортам изделий.

1000 мм · печать 1:1

Изм.	Кол.уч	Лист	№ док.	Подп.	Дата
Разраб.		Кырлан А.С.			04.11.26
Пров.					
ГИП					
Н. контр.					
Утв.					

ГД-2026-010-АИ

Дом 331 м²

Общая площадь 270,67* м² · * размеры приняты, не замерены (реестр — л. 8–10, К-1)

Дизайн-проект интерьера

Стадия	Лист	Листов
РП	167	216

Развёртки стен. Крыльцо (пом. 12)

М 1:20


Кырлан Александр Сергеевич

Развёртка стены А. Спальня мастер (пом. 13)

Спальня мастер (пом. 13) · вид изнутри помещения · размеры в мм, отметки в м от ±0,000 (чистый пол 1-го этажа)


ПРЕДВАРИТЕЛЬНО · не для производства работ · открыто пунктов: 15 (реестр — л. 8–10)

Развёртка стены А

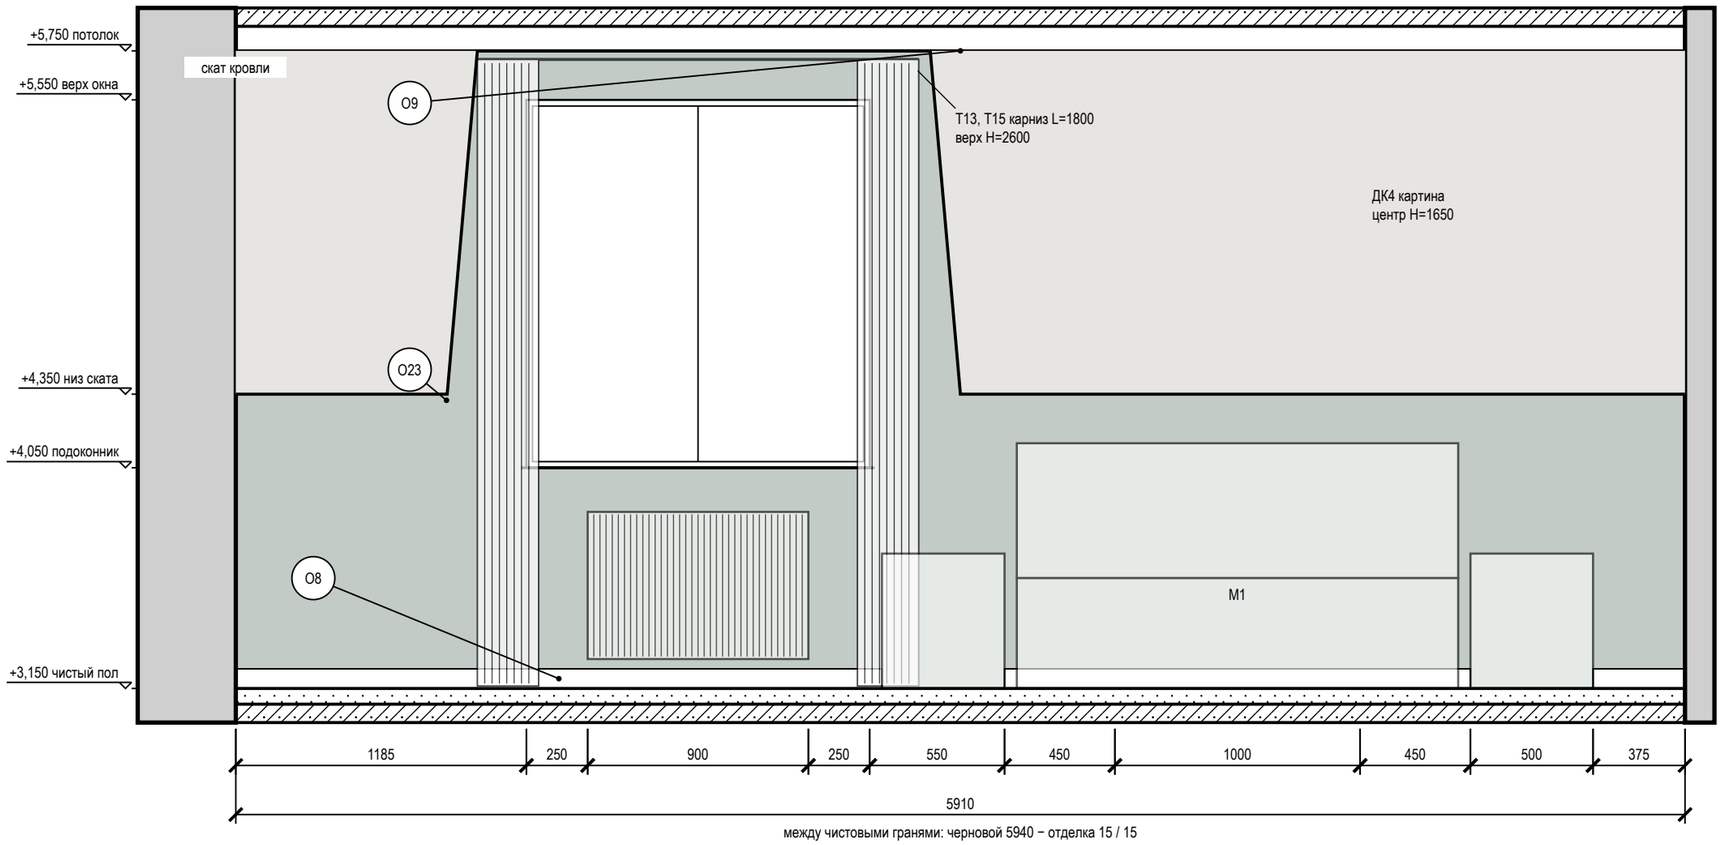

между чистовыми гранями: черновой 5940 − отделка 15 / 15

Схема развёрток (М 1:100)

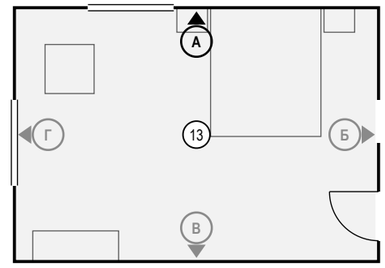

Условные обозначения

- мебель и приборы — фасад по расстановке (условно)
- картина (декор): марка Д, крест — центр, Н — высота центра, мм
- карниз (шина) и шторы в собранном виде: марка Т, длина L, верх Н
- окно: проём, рама, подоконник
- радиатор отопления; марка — по плану отопления
- стены и перекрытия в сечении
- окраска: тон — цвет по коду производителя (условно)
- О1 — марка отделки по реестру отделки альбома
- А — марка развёртки: буква стены, стрелка — взгляд

Ведомость отделки (на листе)

Марка	Поверхность	Материал, изделие	Цвет, код	Кол.
О8	плинтус	плинтус МДФ, h 80 мм, аналог: плинтус МДФ под покраску 80×16	Farrow & Ball No. 226 «Joa's White»	4,9 м
О9	потолок	окраска, Little Greene Absolute Matt, глубокоматовая, подготовка Q3	Little Greene No. 105 «Slaked Lime»	24,6 м²
О23	акцентная стена	окраска, Tikkurila Optiva 5 Matt, матовая, подготовка Q3	NCS S 7020-G10Y «Хвойный тёмно-зелёный»	13,3 м²

Допущения и предложения на листе

Основа листа: размеры и контуры этажей подобраны проектировщиком по составу помещений и площадям этажей с картинки 470 px (размеры на ней не читаются); обмер и исходный проект — задание (К-1); высоты: 1-й этаж 2800 мм, мансарда 2700 мм (горизонтальная часть) приняты; скаты кровли мансарды приняты по картинке: колено 1200 мм, уклон 45°, конёк вдоль длинной стороны; проект КР — задание (К-2); наружные стены 400 мм, перегородки 120 мм приняты (К-1); разрешённая мощность 15 кВт принята по типовым ТУ для частного дома (К-4); подрайон климата не задан — принят не северный (жилые от 2,5 м) (К-7).

Знак «*» — принято, не замерено и не подтверждено (замерить на объекте): К-2: отметка чистого пола этажа «Мансарда» +3,150 — принята без источника, все отметки мансарды считаются от неё.

См. лист открытых вопросов (лист 8, записи К-1, К-2, К-4, К-7).

Примечания

1. Развёртки — вид на стену изнутри помещения, по часовой стрелке; расположение — на схеме листа и на листе 128; размеры — в мм по чистовым поверхностям; отметки — в м от ±0,000 (чистый пол 1-го этажа); высоты Н — от чистого пола помещения до оси изделия, у декора — до центра.
2. Стена А показана двумя видами: здесь — архитектурная развёртка (мебель, отделка, проёмы, высоты), электроточки и выводы ВК с привязками и таблицей — на листе 169 («Привязки»).
3. Схема мебели, приборов и декора не является технической документацией для производства мебели; габариты — по паспортам изделий.
4. Картины и зеркала крепить к основанию по паспорту изделия (закладные и анкеры — в перечне скрытых работ); крест — ось центра предмета.
5. Карнизы (шины) — по ведомости текстиля декоратора: длина L и верх Н на развёртке — те же числа, что в ведомости; крепление — до окраски потолка.
6. Потолок — у каждой стены свой, по плану потолков (ПТ6); ступени — зоной, кромка короба перед нишей — тонкой линией; в поле потолка: ПТ5 +5,650.

1000 мм · печать 1:1

Изм.	Кол.уч	Лист	№ док.	Подп.	Дата
Разраб.		Кырлан А.С.			04.11.26
Пров.					
ГИП					
Н. контр.					
Утв.					

ГД-2026-010-АИ

Дом 331 м²

Общая площадь 270,67* м² · * размеры приняты, не замерены (реестр — л. 8–10, К-1)

Дизайн-проект интерьера	Стадия	Лист	Листов
	РП	168	216

Развёртка стены А. Спальня мастер (пом. 13)

М 1:25

Кырлан Александр Сергеевич

выпуск 04.11.2026 № 2a77323a49 · стр. 172 из 221

Привязки электроточек, стена А. Спальня мастер (пом. 13)

Спальня мастер (пом. 13) · вид изнутри помещения · привязки в мм, отметки в м · к развёртке на листе 168

ПРЕДВАРИТЕЛЬНО · не для производства работ · открыто пунктов: 15 (реестр — л. 8–10)

Развёртка стены А: электроточки и выводы

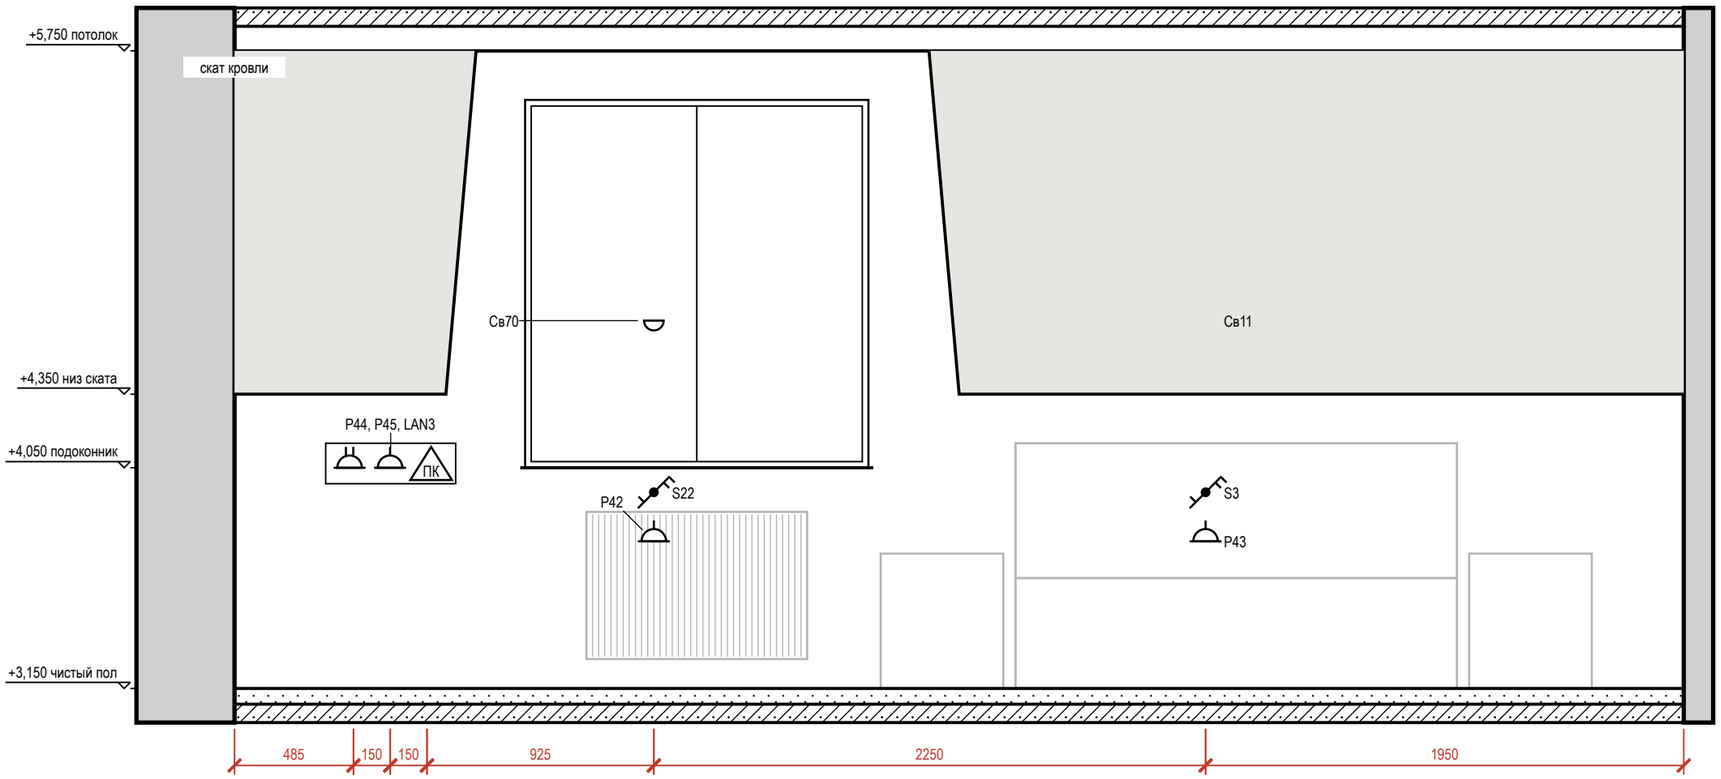


Таблица привязок электроточек и выводов

Марка	Назначение	От угла, мм	Н от пола, мм	Примечание
P44	розетка: рабочий стол	485	900	рамка 2 поста, гр. 4
P45	розетка: рабочий стол	635	900	гр. 4
LAN3	розетка RJ45: рабочий стол	785	900	
P42	розетка: у кровати	1710	600	гр. 4
S22	выключатель	1710	800	гр. 1

Марка	Назначение	От угла, мм	Н от пола, мм	Примечание
Св70	светильник настенный	1710	1500	гр. 1
P43	розетка: у кровати	3960	600	гр. 4
S3	выключатель	3960	800	гр. 1
Св11	светильник настенный	3960	1500	гр. 1

Условные обозначения

- розетка с заземляющим контактом; у знака — марка, ×N постов в рамке, гр. — группа щита, Н — высота оси, мм
- выключатель одноклавишный
- выключатель двухклавишный (флажков — по числу клавиш)
- выключатель с проходной или перекрёстной клавишей (обратный флажок); тип клавиши — в подписи
- светильник настенный (бра), Н — высота оси
- ПК — розетка компьютерная RJ45
- привязки точек и выводов от угла и от пола, мм

Примечания

1. Вид «Привязки» стены А — электроточки и выводы ВК; архитектурная развёртка (мебель, отделка, проёмы, высоты) — на листе 168, расположение — на листе 128. Мебель и приборы — подложкой для ориентира; их марки и обозначения мебели, проёмов и стен — там же.
2. Привязки — в мм: по горизонтали от левого чистового угла стены до оси изделия, Н — от чистого пола до оси; все точки — в таблице привязок. Красная цепочка — привязки по осям; точки ближе 150 мм одна к другой в цепочку не дробятся — их привязки только в таблице.
3. У знака — марка электроточки (Р — розетка, S — выключатель, Св — светильник, ЭВ — вывод кабеля); посты в рамке и группа щита — в графе «Примечание»; группы по клавишам выключателя — на листе выключателей.

Допущения и предложения на листе

Основа листа: размеры и контуры этажей подобраны проектировщиком по составу помещений и площадям этажей с картинки 470 px (размеры на ней не читаются); обмер и исходный проект — задание (К-1); высоты: 1-й этаж 2800 мм, мансарда 2700 мм (горизонтальная часть) приняты; скаты кровли мансарды приняты по картинке: колено 1200 мм, уклон 45°, конёк вдоль длинной стороны; проект КР — задание (К-2); наружные стены 400 мм, перегородки 120 мм приняты (К-1); разрешённая мощность 15 кВт принята по типовым ТУ для частного дома (К-4); подрайон климата не задан — принят не северный (жилые от 2,5 м) (К-7).

Знак «*» — принято, не замерено и не подтверждено (замерить на объекте): К-2: отметка чистого пола этажа «Мансарда» +3,150 — принята без источника, все отметки мансарды считаются от неё.

См. лист открытых вопросов (лист 8, записи К-1, К-2, К-4, К-7).

1000 мм · печать 1:1

Изм.	Кол.уч	Лист	№ док.	Подп.	Дата
Разраб.		Кырлан А.С.			04.11.26
Пров.					
ГИП					
Н. контр.					
Утв.					

ГД-2026-010-АИ

Дом 331 м²

Общая площадь 270,67* м² · * размеры приняты, не замерены (реестр — л. 8–10, К-1)

Дизайн-проект интерьера	Стадия	Лист	Листов
	РП	169	216

Привязки электроточек, стена А. Спальня мастер (пом. 13)

М 1:25

Кырлан Александр Сергеевич


выпуск 04.11.2026 № 2a77323a49 · стр. 173 из 221

Развёртка стены Б. Спальня мастер (пом. 13)

Спальня мастер (пом. 13) · вид изнутри помещения · размеры в мм, отметки в м от ±0,000 (чистый пол 1-го этажа)


ПРЕДВАРИТЕЛЬНО · не для производства работ · открыто пунктов: 15 (реестр — л. 8–10)

Развёртка стены Б

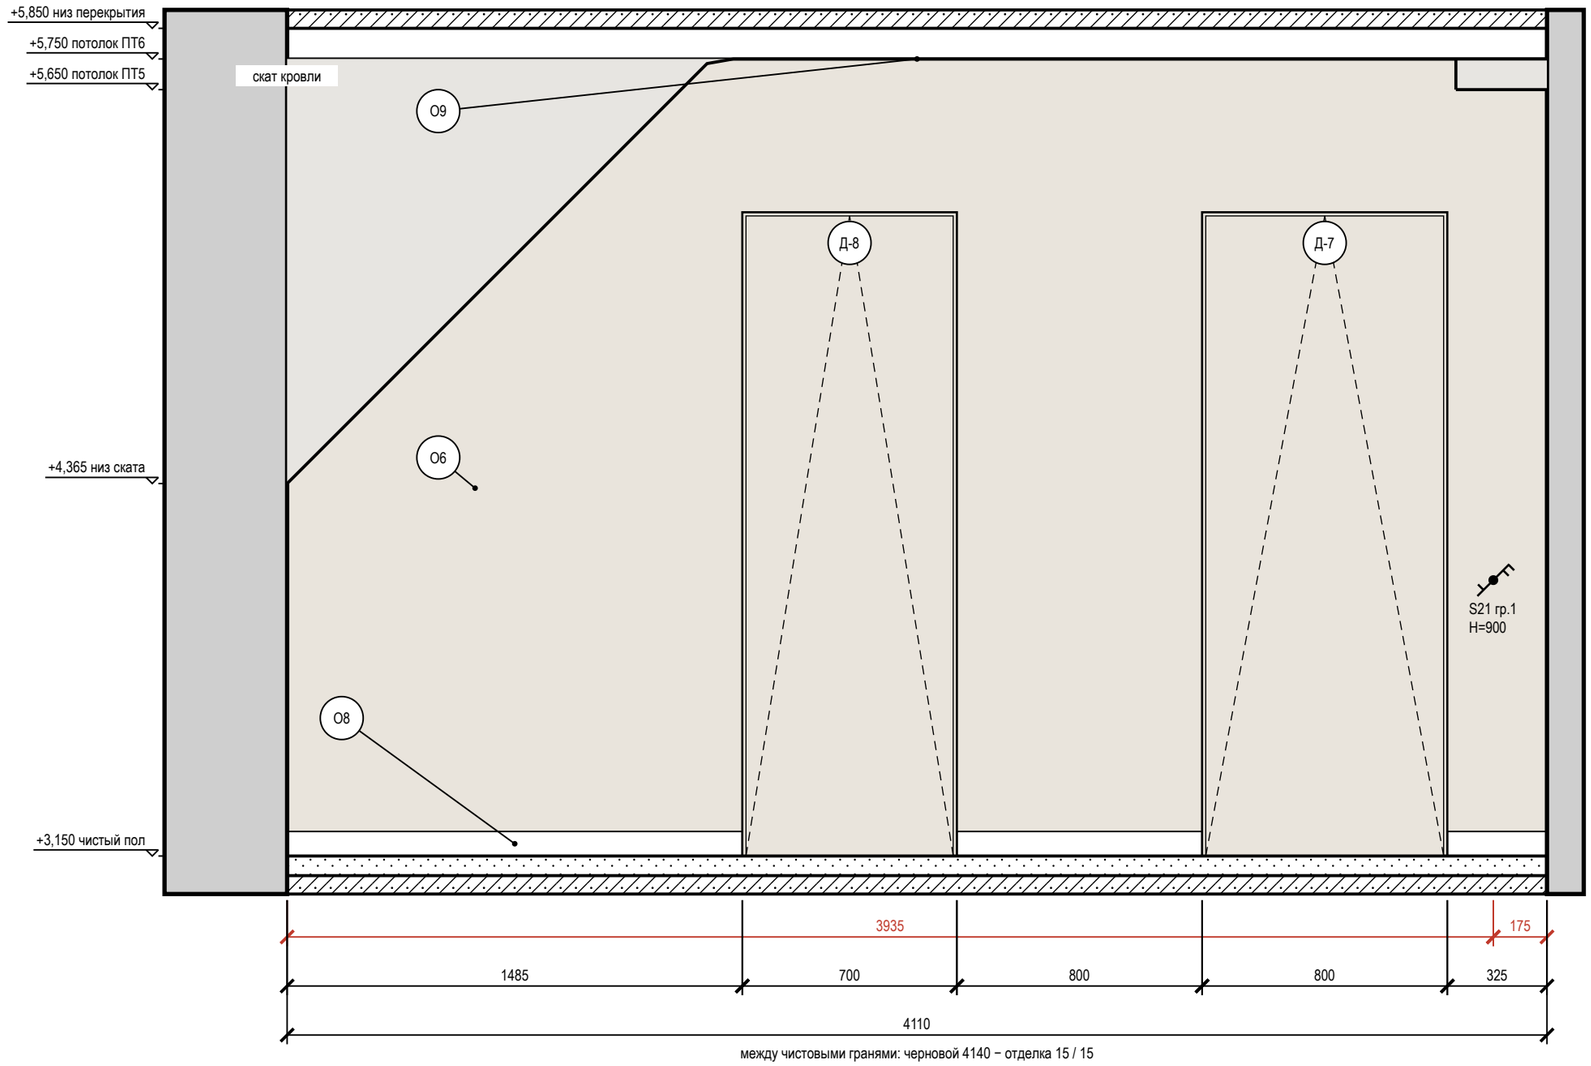

между чистовыми гранями: черновой 4140 − отделка 15 / 15

Схема развёрток (М 1:100)

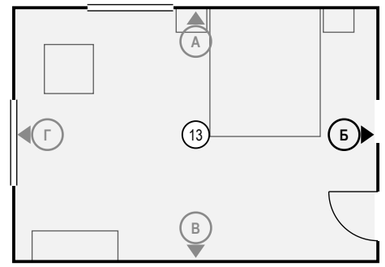

Условные обозначения

- выключатель одноклавишный
- выключатель двухклавишный (флажков — по числу клавиш)
- выключатель с проходной или перекрёстной клавишей (обратный флажок); тип клавиши — в подписи
- привязки точек и выводов от угла и от пола, мм
- мебель и приборы — фасад по расстановке (условно)
- дверь скрытого монтажа: полотно в плоскости стены (узел — на листе узлов)
- стены и перекрытия в сечении
- окраска: тон — цвет по коду производителя (условно)
- О1 — марка отделки по реестру отделки альбома
- А — марка развёртки: буква стены, стрелка — взгляд

Ведомость отделки (на листе)

Марка	Поверхность	Материал, изделие	Цвет, код	Кол.
О6	стены	окраска, Farrow & Ball Modern Emulsion, матовая, подготовка Q3	Farrow & Ball No. 226 «Joa's White»	7,5 м²
О8	плинтус	плинтус МДФ, h 80 мм, аналог: плинтус МДФ под покраску 80×16	Farrow & Ball No. 226 «Joa's White»	2,6 м
О9	потолок	окраска, Little Greene Absolute Matt, глубокоматовая, подготовка Q3	Little Greene No. 105 «Slaked Lime»	24,6 м²

Допущения и предложения на листе

Основа листа: размеры и контуры этажей подобраны проектировщиком по составу помещений и площадям этажей с картинки 470 px (размеры на ней не читаются); обмер и исходный проект — задание (К-1); высоты: 1-й этаж 2800 мм, мансарда 2700 мм (горизонтальная часть) приняты; скаты кровли мансарды приняты по картинке: колено 1200 мм, уклон 45°, конёк вдоль длинной стороны; проект КР — задание (К-2); наружные стены 400 мм, перегородки 120 мм приняты (К-1); разрешённая мощность 15 кВт принята по типовым ТУ для частного дома (К-4); подрайон климата не задан — принят не северный (жилые от 2,5 м) (К-7).

Знак «*» — принято, не замерено и не подтверждено (замерить на объекте): К-2: отметка чистого пола этажа «Мансарда» +3,150 — принята без источника, все отметки мансарды считаются от неё. См. лист открытых вопросов (лист 8, записи К-1, К-2, К-4, К-7).

Примечания

1. Развёртки — вид на стену изнутри помещения, по часовой стрелке; расположение — на схеме листа и на листе 128; размеры — в мм по чистовым поверхностям; отметки — в м от ±0,000 (чистый пол 1-го этажа); высоты Н — от чистого пола помещения до оси изделия, у декора — до центра.
2. Красная цепочка — привязки электроточек и выводов по осям от угла чистовых стен; высота Н — у знака, от чистого пола до оси; высоты мебели, проёмов и границ отделки — колонкой отметок слева. Стена с 5 и более точками или с мелкими звеньями привязок показана двумя видами: архитектурная развёртка (мебель, отделка, проёмы, высоты) и вид «Привязки» на отдельном листе — точки и выводы с марками, одна цепочка по осям и таблица привязок (каждая точка — строка).
3. У знака электроточки: марка (Р — розетка, S — выключатель, Св — светильник, ЭВ — вывод кабеля), ×N — число постов в рамке, гр. — группа щита, Н — высота оси от чистого пола, мм; группы по клавишам выключателя — на листе выключателей.
4. Схема мебели, приборов и декора не является технической документацией для производства мебели; габариты — по паспортам изделий.
5. Двери скрытого монтажа — полотно в плоскости стены, отделка стены по полотну, плинтус прерывается у короба (узел — на листе узлов).
6. Потолок — у каждой стены свой, по плану потолков (ПТ6, ПТ5); ступени — зоной, кромка короба перед нишей — тонкой линией.

1000 мм · печать 1:1

Изм.	Кол.уч	Лист	№ док.	Подп.	Дата
Разраб.		Кырлан А.С.			04.11.26
Пров.					
ГИП					
Н. контр.					
Утв.					

ГД-2026-010-АИ

Дом 331 м²

Общая площадь 270,67* м² · * размеры приняты, не замерены (реестр — л. 8–10, К-1)

Дизайн-проект интерьера	Стадия	Лист	Листов
	РП	170	216

Развёртка стены Б. Спальня мастер (пом. 13)

М 1:20

Кырлан Александр Сергеевич


выпуск 04.11.2026 № 2a77323a49 · стр. 174 из 221

Развёртка стены В. Спальня мастер (пом. 13)

Спальня мастер (пом. 13) · вид изнутри помещения · размеры в мм, отметки в м от ±0,000 (чистый пол 1-го этажа)


ПРЕДВАРИТЕЛЬНО · не для производства работ · открыто пунктов: 15 (реестр — л. 8–10)

Развёртка стены В

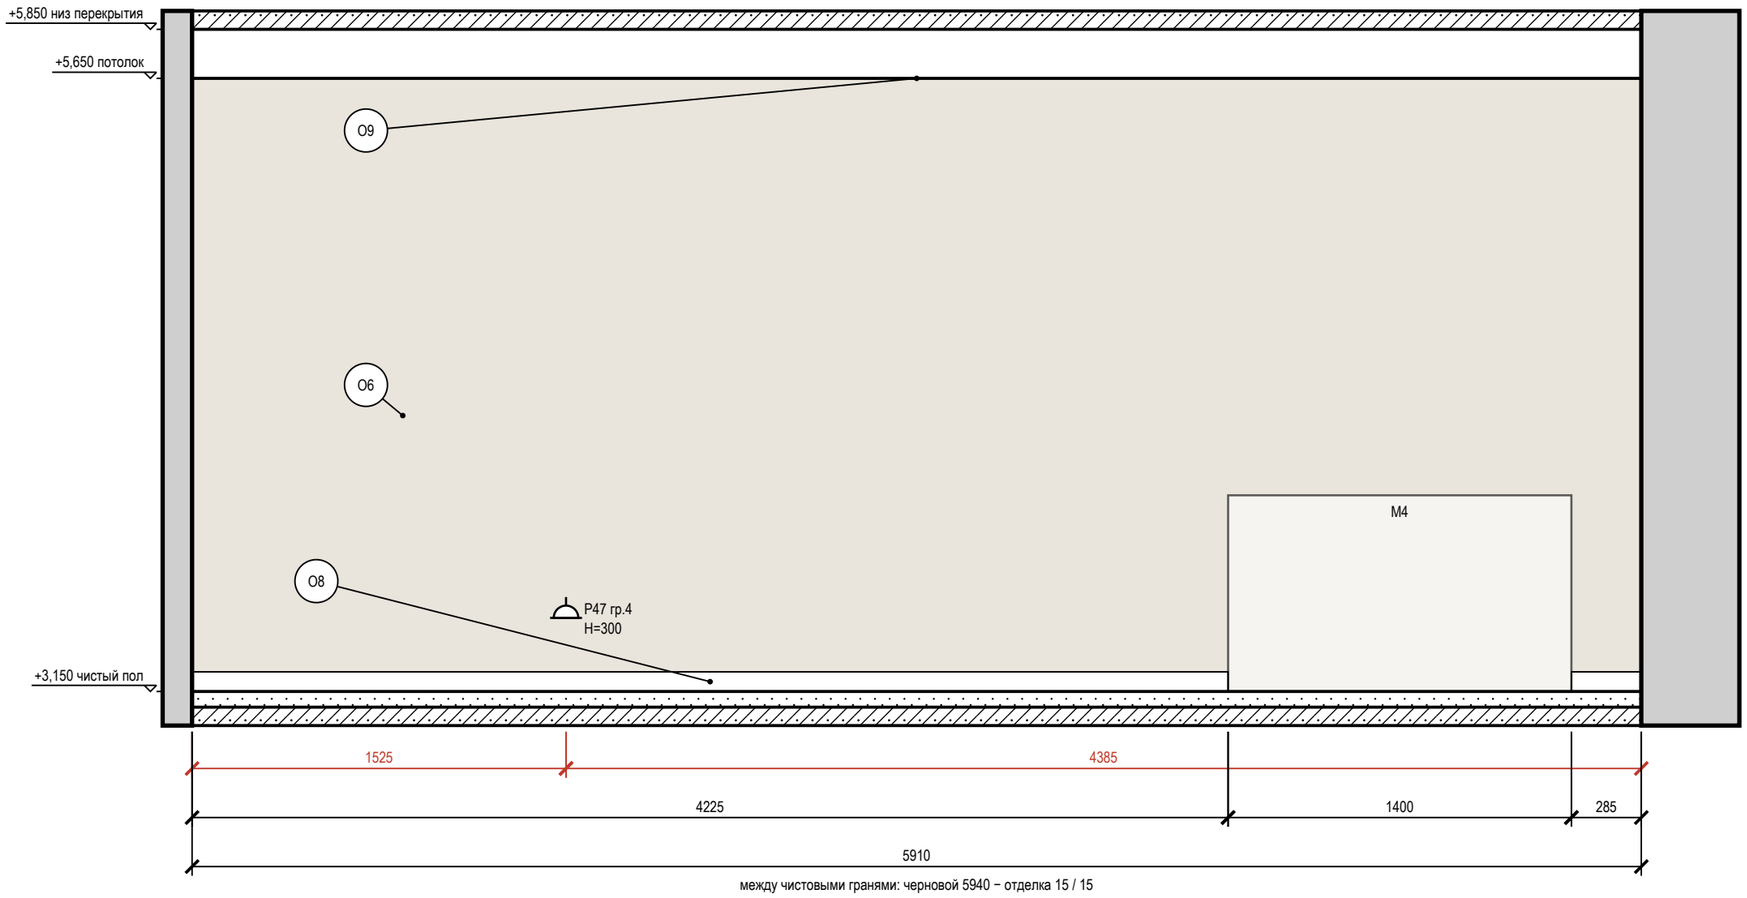

между чистовыми гранями: черновой 5940 − отделка 15 / 15

Схема развёрток (М 1:100)

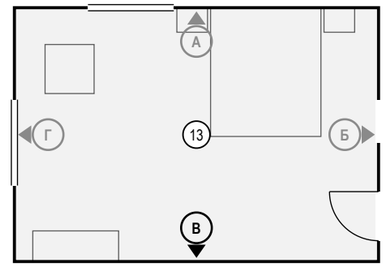

Условные обозначения

- розетка с заземляющим контактом; у знака — марка, ×N постов в рамке, гр. — группа щита, Н — высота оси, мм
- привязки точек и выводов от угла и от пола, мм
- мебель и приборы — фасад по расстановке (условно)
- стены и перекрытия в сечении
- окраска: тон — цвет по коду производителя (условно)
- О1 — марка отделки по реестру отделки альбома
- А — марка развёртки: буква стены, стрелка — взгляд

Ведомость отделки (на листе)

Марка	Поверхность	Материал, изделие	Цвет, код	Кол.
О6	стены	окраска, Farrow & Ball Modern Emulsion, матовая, подготовка Q3	Farrow & Ball No. 226 «Joa's White»	14,8 м²
О8	плинтус	плинтус МДФ, h 80 мм, аналог: плинтус МДФ под покраску 80×16	Farrow & Ball No. 226 «Joa's White»	4,5 м
О9	потолок	окраска, Little Greene Absolute Matt, глубокоматовая, подготовка Q3	Little Greene No. 105 «Slaked Lime»	24,6 м²

Допущения и предложения на листе

Основа листа: размеры и контуры этажей подобраны проектировщиком по составу помещений и площадям этажей с картинки 470 px (размеры на ней не читаются); обмер и исходный проект — задание (К-1); высоты: 1-й этаж 2800 мм, мансарда 2700 мм (горизонтальная часть) приняты; скаты кровли мансарды приняты по картинке: колено 1200 мм, уклон 45°, конёк вдоль длинной стороны; проект КР — задание (К-2); наружные стены 400 мм, перегородки 120 мм приняты (К-1); разрешённая мощность 15 кВт принята по типовым ТУ для частного дома (К-4); подрайон климата не задан — принят не северный (жилые от 2,5 м) (К-7).

Знак «*» — принято, не замерено и не подтверждено (замерить на объекте): К-2: отметка чистого пола этажа «Мансарда» +3,150 — принята без источника, все отметки мансарды считаются от неё.

См. лист открытых вопросов (лист 8, записи К-1, К-2, К-4, К-7).

Примечания

1. Развёртки — вид на стену изнутри помещения, по часовой стрелке; расположение — на схеме листа и на листе 128; размеры — в мм по чистовым поверхностям; отметки — в м от ±0,000 (чистый пол 1-го этажа); высоты Н — от чистого пола помещения до оси изделия, у декора — до центра.
2. Красная цепочка — привязки электроточек и выводов по осям от угла чистовых стен; высота Н — у знака, от чистого пола до оси; высоты мебели, проёмов и границ отделки — колонкой отметок слева. Стена с 5 и более точками или с мелкими звеньями привязок показана двумя видами: архитектурная развёртка (мебель, отделка, проёмы, высоты) и вид «Привязки» на отдельном листе — точки и выводы с марками, одна цепочка по осям и таблица привязок (каждая точка — строка).
3. У знака электроточки: марка (Р — розетка, S — выключатель, Св — светильник, ЭВ — вывод кабеля), ×N — число постов в рамке, гр. — группа щита, Н — высота оси от чистого пола, мм; группы по клавишам выключателя — на листе выключателей.
4. Схема мебели, приборов и декора не является технической документацией для производства мебели; габариты — по паспортам изделий.
5. Потолок — у каждой стены свой, по плану потолков (ПТ5); ступени — зоной, кромка короба перед нишей — тонкой линией; в поле потолка: ПТ6 +5,750.

1000 мм · печать 1:1

Изм.	Кол.уч	Лист	№ док.	Подп.	Дата
Разраб.		Кырлан А.С.			04.11.26
Пров.					
ГИП					
Н. контр.					
Утв.					

ГД-2026-010-АИ

Дом 331 м²

Общая площадь 270,67* м² · * размеры приняты, не замерены (реестр — л. 8–10, К-1)

Дизайн-проект интерьера

Стадия	Лист	Листов
РП	171	216

Развёртка стены В. Спальня мастер (пом. 13)

М 1:25

Кырлан Александр Сергеевич


выпуск 04.11.2026 № 2a77323a49 · стр. 175 из 221

Развёртка стены Г. Спальня мастер (пом. 13)

Спальня мастер (пом. 13) · вид изнутри помещения · размеры в мм, отметки в м от ±0,000 (чистый пол 1-го этажа)

ПРЕДВАРИТЕЛЬНО · не для производства работ · открыто пунктов: 15 (реестр — л. 8–10)

Развёртка стены Г

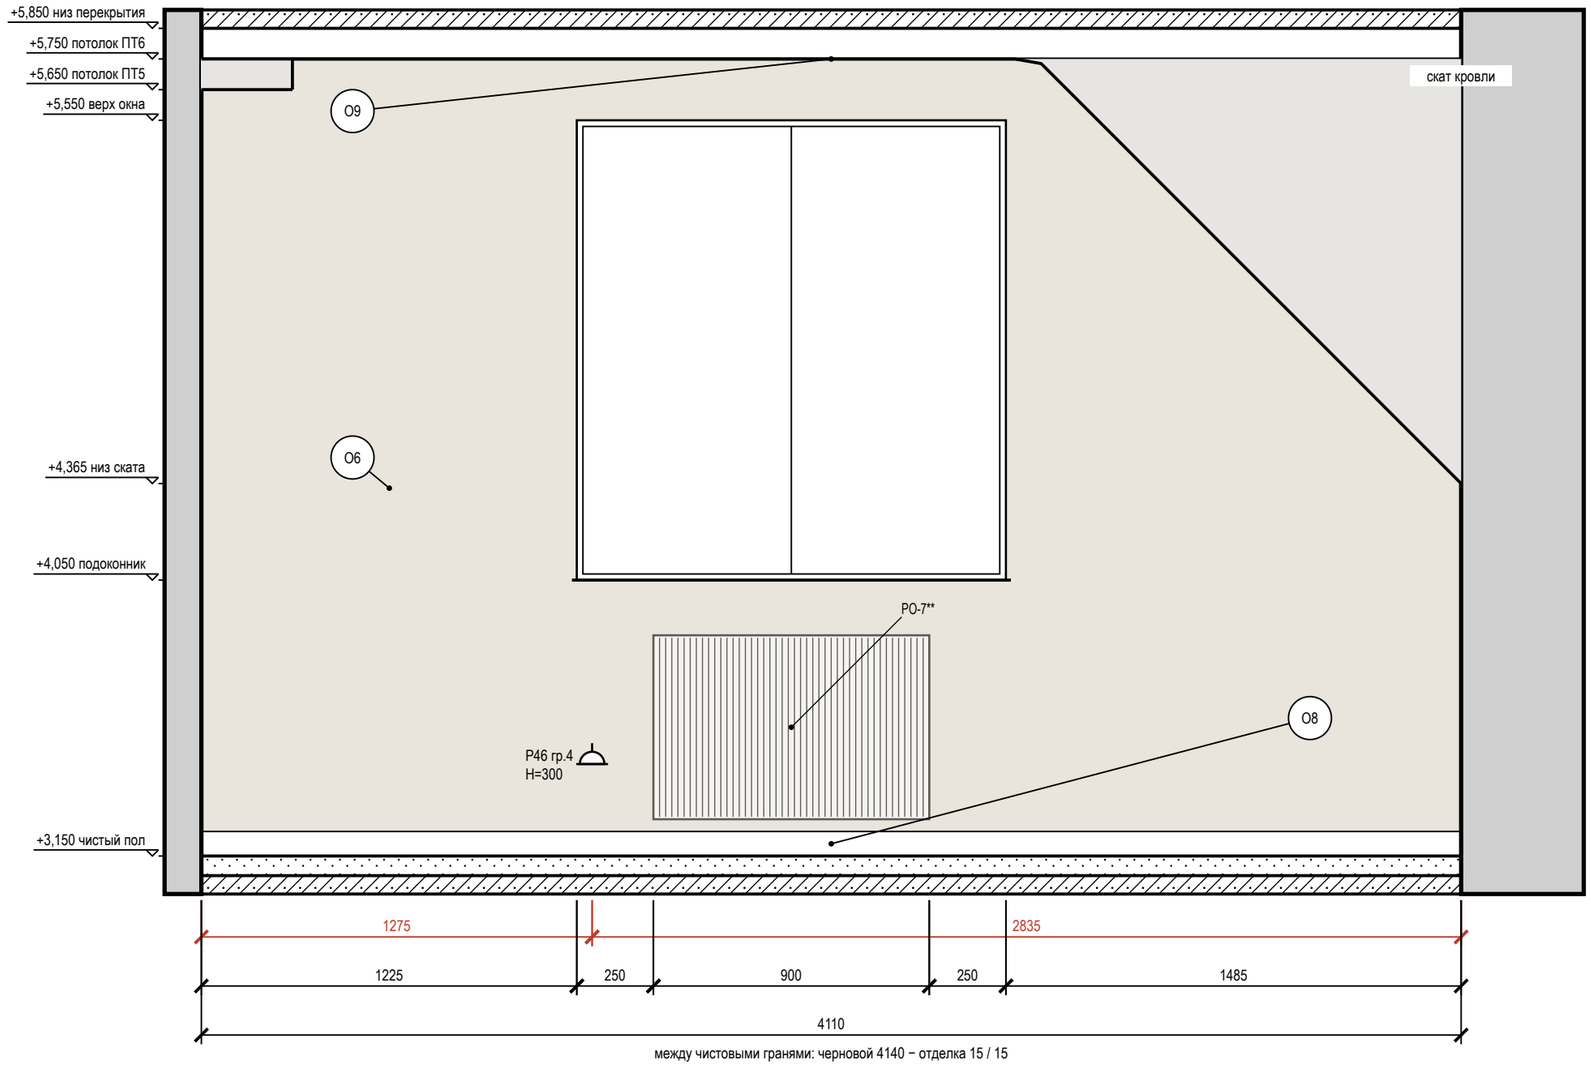

между чистовыми гранями: черновой 4140 − отделка 15 / 15


Допущения и предложения на листе. Основа листа: размеры и контуры этажей подобраны проектировщиком по составу помещений и площадям этажей с картинки 470 px (размеры на ней не читаются); обмер и исходный проект — задание (К-1); высоты: 1-й этаж 2800 мм, мансарда 2700 мм (горизонтальная часть) приняты; скаты кровли мансарды приняты по картинке: колено 1200 мм, уклон 45°, конёк вдоль длинной стороны; проект КР — задание (К-2); наружные стены 400 мм, перегородки 120 мм приняты (К-1); разрешённая мощность 15 кВт принята по типовым ТУ для частного дома (К-4); подрайон климата не задан — принят не северный (жилые от 2,5 м) (К-7). Знак «*» — принято, не замерено и не подтверждено (замерить на объекте): К-2: отметка чистого пола этажа «Мансарда» +3,150 — принята без источника, все отметки мансарды считаются от неё. Знак «**» — предложение проектировщика, заказчиком не утверждено (согласовать с заказчиком): К-11: РО-7 — прибор под окном по оси проёма, ширина ≈ 0,7 ширины окна — предложение ОВ (лист ОВ выводил его сам до, теперь он в данных — один источник для листа, мебели, DXF и IFC); котёл и мощность не выбраны (К-11) — размер по теплотехническому расчёту. См. лист открытых вопросов (лист 8, записи К-1, К-2, К-4, К-7; лист 9, запись К-11).

Примечания

1. Развёртки — вид на стену изнутри помещения, по часовой стрелке; расположение — на схеме листа и на листе 128; размеры — в мм по чистовым поверхностям; отметки — в м от ±0,000 (чистый пол 1-го этажа); высоты Н — от чистого пола помещения до оси изделия, у декора — до центра.
2. Красная цепочка — привязки электроточек и выводов по осям от угла чистовых стен; высота Н — у знака, от чистого пола до оси; высоты мебели, проёмов и границ отделки — колонкой отметок слева. Стена с 5 и более точками или с мелкими звеньями привязок показана двумя видами: архитектурная развёртка (мебель, отделка, проёмы, высоты) и вид «Привязки» на отдельном листе — точки и выводы с марками, одна цепочка по осям и таблица привязок (каждая точка — строка).
3. У знака электроточки: марка (Р — розетка, S — выключатель, Св — светильник, ЭВ — вывод кабеля), ×N — число постов в рамке, гр. — группа щита, Н — высота оси от чистого пола, мм; группы по клавишам выключателя — на листе выключателей.
4. Схема мебели, приборов и декора не является технической документацией для производства мебели; габариты — по паспортам изделий.
5. Потолок — у каждой стены свой, по плану потолков (ПТ6, ПТ5); ступени — зоной, кромка короба перед нишей — тонкой линией.

1000 мм · печать 1:1

Схема развёрток (М 1:100)

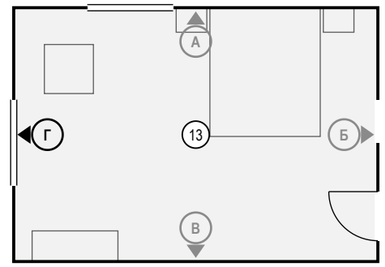

Условные обозначения

- розетка с заземляющим контактом; у знака — марка, ×N постов в рамке, гр. — группа щита, Н — высота оси, мм
- привязки точек и выводов от угла и от пола, мм
- мебель и приборы — фасад по расстановке (условно)
- окно: проём, рама, подоконник
- радиатор отопления; марка — по плану отопления
- стены и перекрытия в сечении
- окраска: тон — цвет по коду производителя (условно)
- О1 — марка отделки по реестру отделки альбома
- А — марка развёртки: буква стены, стрелка — взгляд

Ведомость отделки (на листе)

Марка	Поверхность	Материал, изделие	Цвет, код	Кол.
О6	стены	окраска, Farrow & Ball Modern Emulsion, матовая, подготовка Q3	Farrow & Ball No. 226 «Joa's White»	8,6 м²
О8	плинтус	плинтус МДФ, h 80 мм, аналог: плинтус МДФ под покраску 80×16	Farrow & Ball No. 226 «Joa's White»	4,1 м
О9	потолок	окраска, Little Greene Absolute Matt, глубокоматовая, подготовка Q3	Little Greene No. 105 «Slaked Lime»	24,6 м²

Изм.	Кол.уч	Лист	№ док.	Подп.	Дата
Разраб.		Кырлан А.С.			04.11.26
Пров.					
ГИП					
Н. контр.					
Утв.					

ГД-2026-010-АИ

Дом 331 м²

Общая площадь 270,67* м² · * размеры приняты, не замерены (реестр — л. 8–10, К-1)

Дизайн-проект интерьера

Стадия	Лист	Листов
РП	172	216

Развёртка стены Г. Спальня мастер (пом. 13)

М 1:20

Кырлан Александр Сергеевич


выпуск 04.11.2026 № 2a77323a49 · стр. 176 из 221

Развёртки стен А, Б. Гардеробная мастер (пом. 14)

Гардеробная мастер (пом. 14) · вид изнутри помещения · размеры в мм, отметки в м от ±0,000 (чистый пол 1-го этажа)


ПРЕДВАРИТЕЛЬНО · не для производства работ · открыто пунктов: 15 (реестр — л. 8–10)

Развёртка стены А

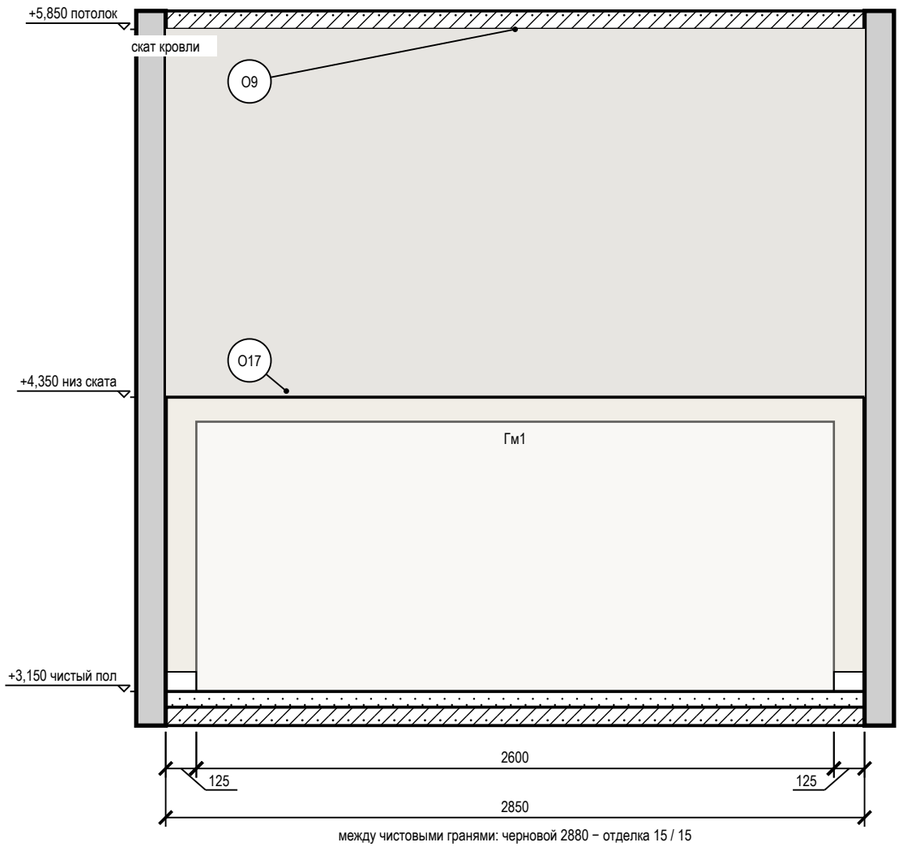

между чистовыми гранями: черновой 2880 − отделка 15 / 15

Развёртка стены Б

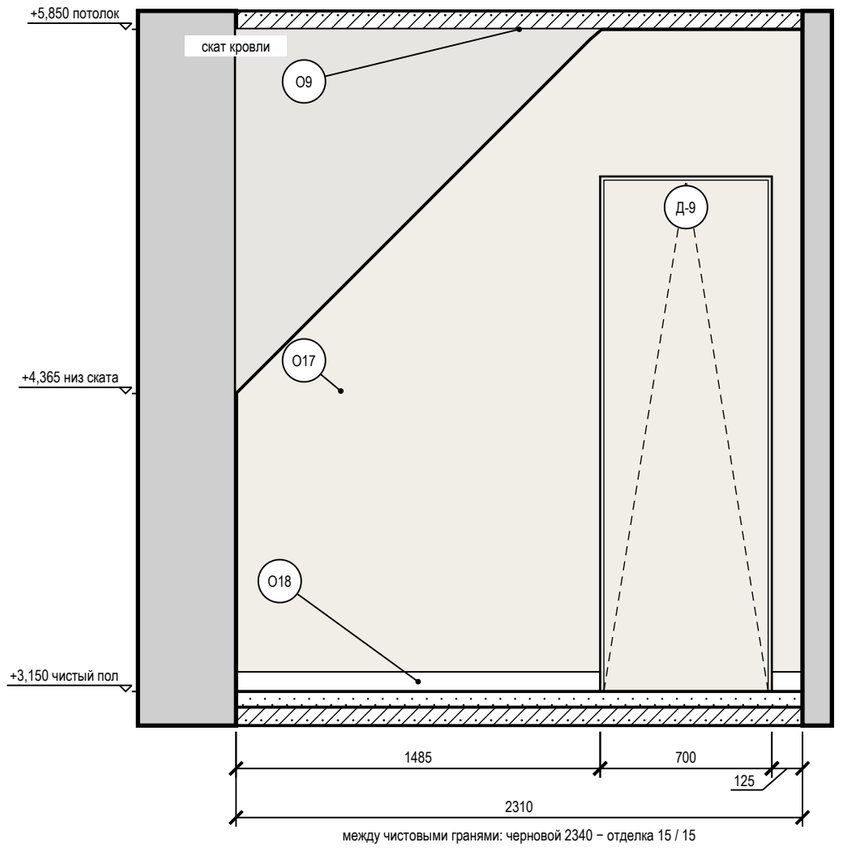


между чистовыми гранями: черновой 2340 − отделка 15 / 15

Условные обозначения

- мебель и приборы — фасад по расстановке (условно)
- дверь скрытого монтажа: полотно в плоскости стены (узел — на листе узлов)
- стены и перекрытия в сечении
- окраска: тон — цвет по коду производителя (условно)
- О1 — марка отделки по реестру отделки альбома
- А — марка развёртки: буква стены, стрелка — взгляд

Схема развёрток (М 1:100)

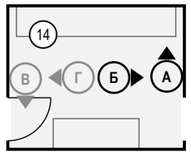

Ведомость отделки (на листе)

Марка	Поверхность	Материал, изделие	Цвет, код	Кол.
О9	потолок	окраска, Little Greene Absolute Matt, глубокоматовая, подготовка Q3	Little Greene No. 105 «Slaked Lime»	6,7 м²
О17	стены	окраска, Little Greene Intelligent Matt, матовая, подготовка Q3	Little Greene No. 105 «Slaked Lime»	12,5 м²
О18	плинтус	плинтус МДФ, h 80 мм, аналог: плинтус МДФ под покраску 80×16	Little Greene No. 105 «Slaked Lime»	1,9 м

Допущения и предложения на листе

Основа листа: размеры и контуры этажей подобраны проектировщиком по составу помещений и площадям этажей с картинки 470 px (размеры на ней не читаются); обмер и исходный проект — задание (К-1); высоты: 1-й этаж 2800 мм, мансарда 2700 мм (горизонтальная часть) приняты; скаты кровли мансарды приняты по картинке: колено 1200 мм, уклон 45°, конёк вдоль длинной стороны; проект КР — задание (К-2); наружные стены 400 мм, перегородки 120 мм приняты (К-1); разрешённая мощность 15 кВт принята по типовым ТУ для частного дома (К-4); подрайон климата не задан — принят не северный (жилые от 2,5 м) (К-7).
Знак «*» — принято, не замерено и не подтверждено (замерить на объекте): К-2: отметка чистого пола этажа «Мансарда» +3,150 — принята без источника, все отметки мансарды считаются от неё.
См. лист открытых вопросов (лист 8, записи К-1, К-2, К-4, К-7).

Примечания

1. Развёртки — вид на стену изнутри помещения, по часовой стрелке; расположение — на схеме листа и на листе 128; размеры — в мм по чистовым поверхностям; отметки — в м от ±0,000 (чистый пол 1-го этажа); высоты Н — от чистого пола помещения до оси изделия, у декора — до центра.
2. Схема мебели, приборов и декора не является технической документацией для производства мебели; габариты — по паспортам изделий.
3. Двери скрытого монтажа — полотно в плоскости стены, отделка стены по полотну, плинтус прерывается у короба (узел — на листе узлов).

1000 мм · печать 1:1

Изм.	Кол.уч	Лист	№ док.	Подп.	Дата
Разраб.		Кырлан А.С.			04.11.26
Пров.					
ГИП					
Н. контр.					
Утв.					

ГД-2026-010-АИ

Дом 331 м²

Общая площадь 270,67* м² · * размеры приняты, не замерены (реестр — л. 8–10, К-1)

Дизайн-проект интерьера

Стадия	Лист	Листов
РП	173	216

Развёртки стен А, Б. Гардеробная мастер (пом. 14)

М 1:25

Кырлан Александр Сергеевич


выпуск 04.11.2026 № 2a77323a49 · стр. 177 из 221

Развёртки стен В, Г. Гардеробная мастер (пом. 14)

Гардеробная мастер (пом. 14) · вид изнутри помещения · размеры в мм, отметки в м от ±0,000 (чистый пол 1-го этажа)


ПРЕДВАРИТЕЛЬНО · не для производства работ · открыто пунктов: 15 (реестр — л. 8–10)

Развёртка стены В

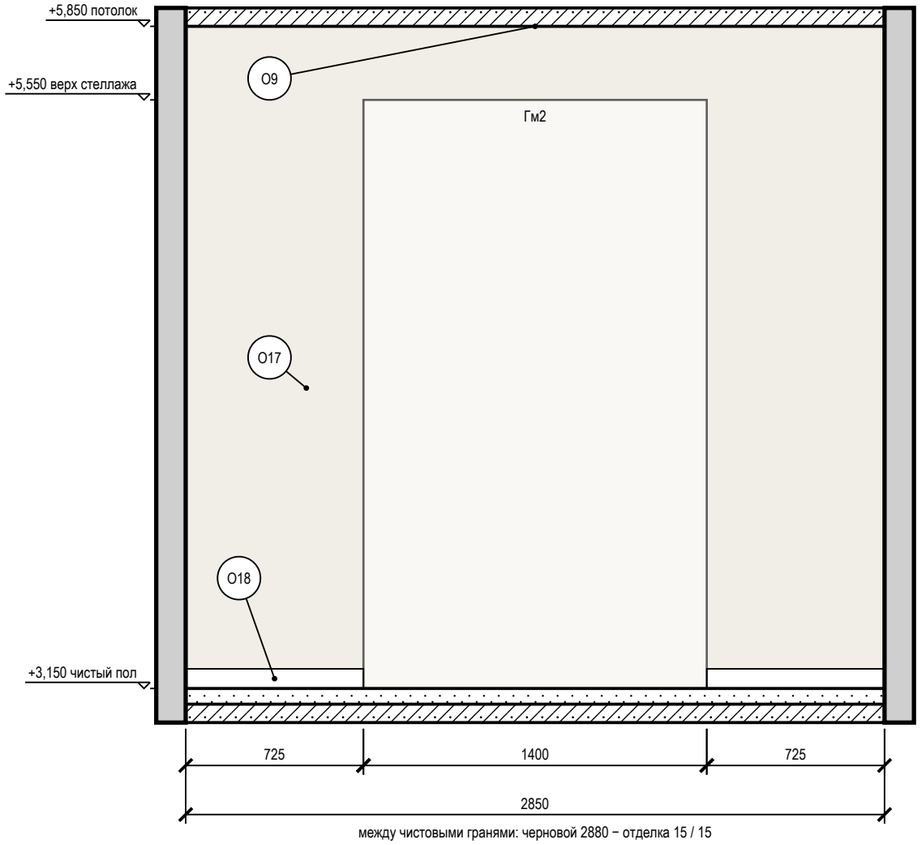

между чистовыми гранями: черновой 2880 − отделка 15 / 15

Развёртка стены Г

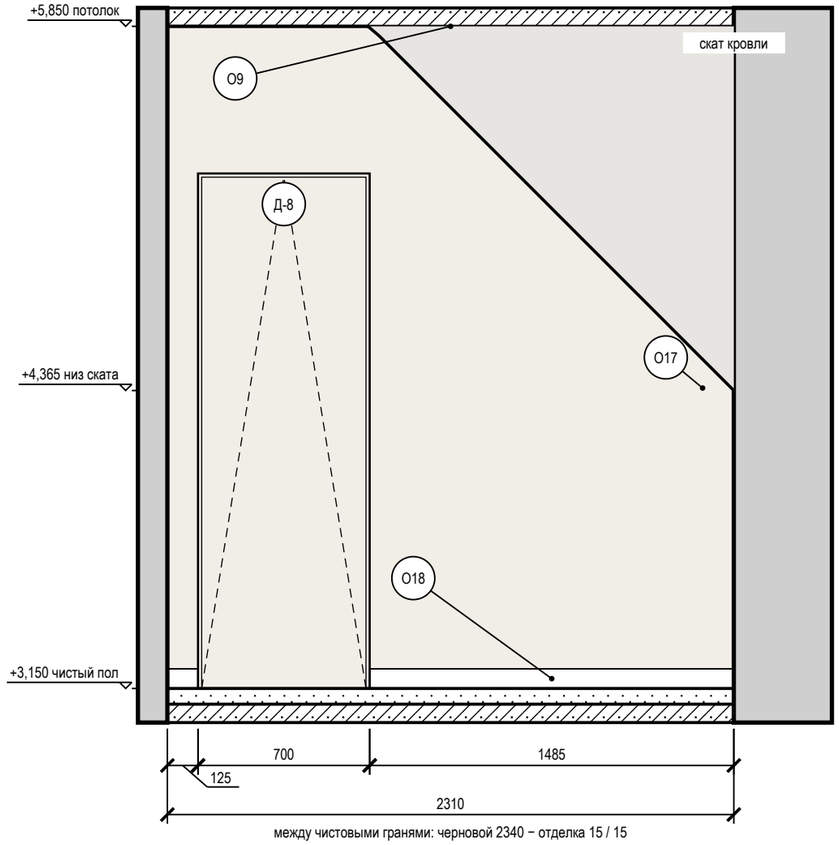


между чистовыми гранями: черновой 2340 − отделка 15 / 15

Условные обозначения

- мебель и приборы — фасад по расстановке (условно)
- дверь скрытого монтажа: полотно в плоскости стены (узел — на листе узлов)
- стены и перекрытия в сечении
- окраска: тон — цвет по коду производителя (условно)
- О1 — марка отделки по реестру отделки альбома
- А — марка развёртки: буква стены, стрелка — взгляд

Схема развёрток (М 1:100)

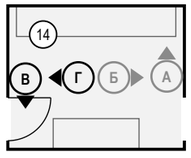

Ведомость отделки (на листе)

Марка	Поверхность	Материал, изделие	Цвет, код	Кол.
О9	потолок	окраска, Little Greene Absolute Matt, глубокоматовая, подготовка Q3	Little Greene No. 105 «Slaked Lime»	6,7 м²
О17	стены	окраска, Little Greene Intelligent Matt, матовая, подготовка Q3	Little Greene No. 105 «Slaked Lime»	12,5 м²
О18	плинтус	плинтус МДФ, h 80 мм, аналог: плинтус МДФ под покраску 80×16	Little Greene No. 105 «Slaked Lime»	3,1 м

Допущения и предложения на листе

Основа листа: размеры и контуры этажей подобраны проектировщиком по составу помещений и площадям этажей с картинки 470 px (размеры на ней не читаются); обмер и исходный проект — задание (К-1); высоты: 1-й этаж 2800 мм, мансарда 2700 мм (горизонтальная часть) приняты; скаты кровли мансарды приняты по картинке: колено 1200 мм, уклон 45°, конёк вдоль длинной стороны; проект КР — задание (К-2); наружные стены 400 мм, перегородки 120 мм приняты (К-1); разрешённая мощность 15 кВт принята по типовым ТУ для частного дома (К-4); подрайон климата не задан — принят не северный (жилые от 2,5 м) (К-7).
Знак «*» — принято, не замерено и не подтверждено (замерить на объекте): К-2: отметка чистого пола этажа «Мансарда» +3,150 — принята без источника, все отметки мансарды считаются от неё.
См. лист открытых вопросов (лист 8, записи К-1, К-2, К-4, К-7).

Примечания

1. Развёртки — вид на стену изнутри помещения, по часовой стрелке; расположение — на схеме листа и на листе 128; размеры — в мм по чистовым поверхностям; отметки — в м от ±0,000 (чистый пол 1-го этажа); высоты Н — от чистого пола помещения до оси изделия, у декора — до центра.
2. Схема мебели, приборов и декора не является технической документацией для производства мебели; габариты — по паспортам изделий.
3. Двери скрытого монтажа — полотно в плоскости стены, отделка стены по полотну, плинтус прерывается у короба (узел — на листе узлов).

1000 мм · печать 1:1

Изм.	Кол.уч	Лист	№ док.	Подп.	Дата
Разраб.		Кырлан А.С.			04.11.26
Пров.					
ГИП					
Н. контр.					
Утв.					

ГД-2026-010-АИ

Дом 331 м²

Общая площадь 270,67* м² · * размеры приняты, не замерены (реестр — л. 8–10, К-1)

Дизайн-проект интерьера

Стадия	Лист	Листов
РП	174	216

Развёртки стен В, Г. Гардеробная мастер (пом. 14)

М 1:25

Кырлан Александр Сергеевич


выпуск 04.11.2026 № 2a77323a49 · стр. 178 из 221

Развёртки стен А, Б. Санузел мастер (пом. 15)

Санузел мастер (пом. 15) · вид изнутри помещения · размеры в мм, отметки в м от ±0,000 (чистый пол 1-го этажа)


ПРЕДВАРИТЕЛЬНО · не для производства работ · открыто пунктов: 15 (реестр — л. 8–10)

Развёртка стены А

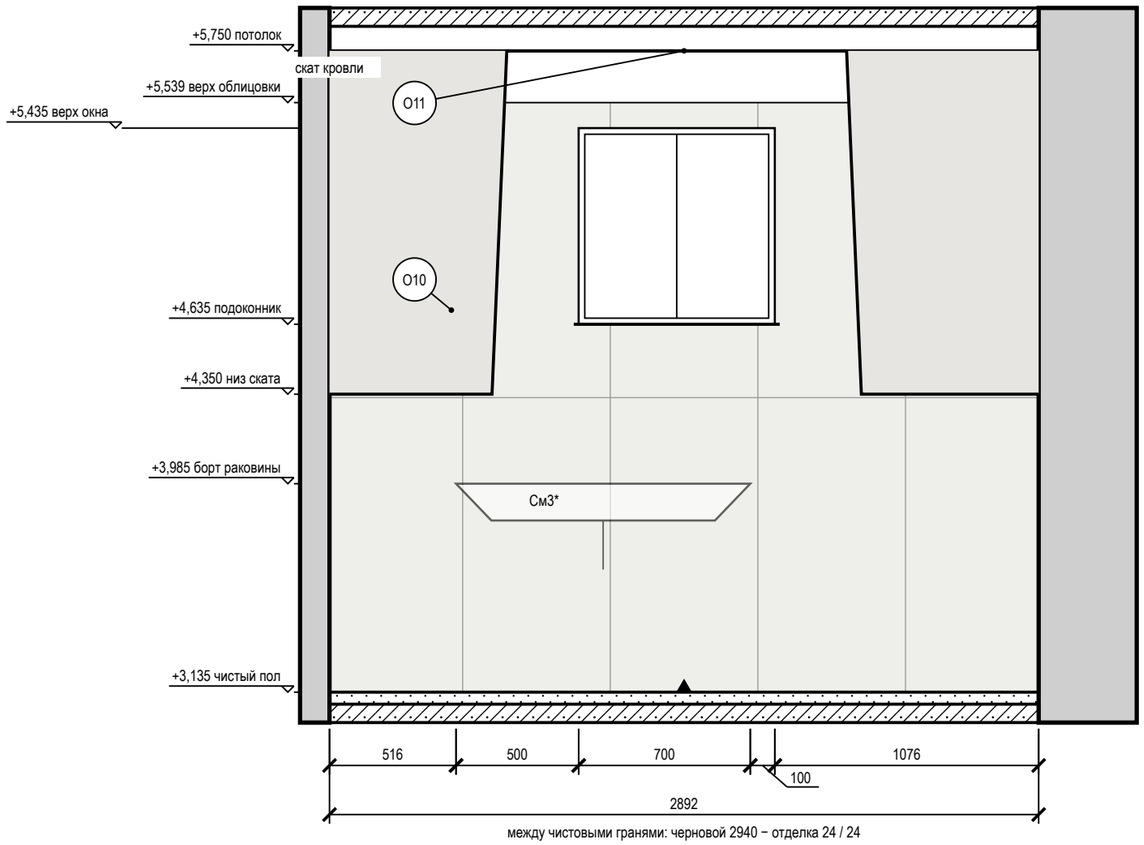


между чистовыми гранями: черновой 2940 − отделка 24 / 24

Развёртка стены Б

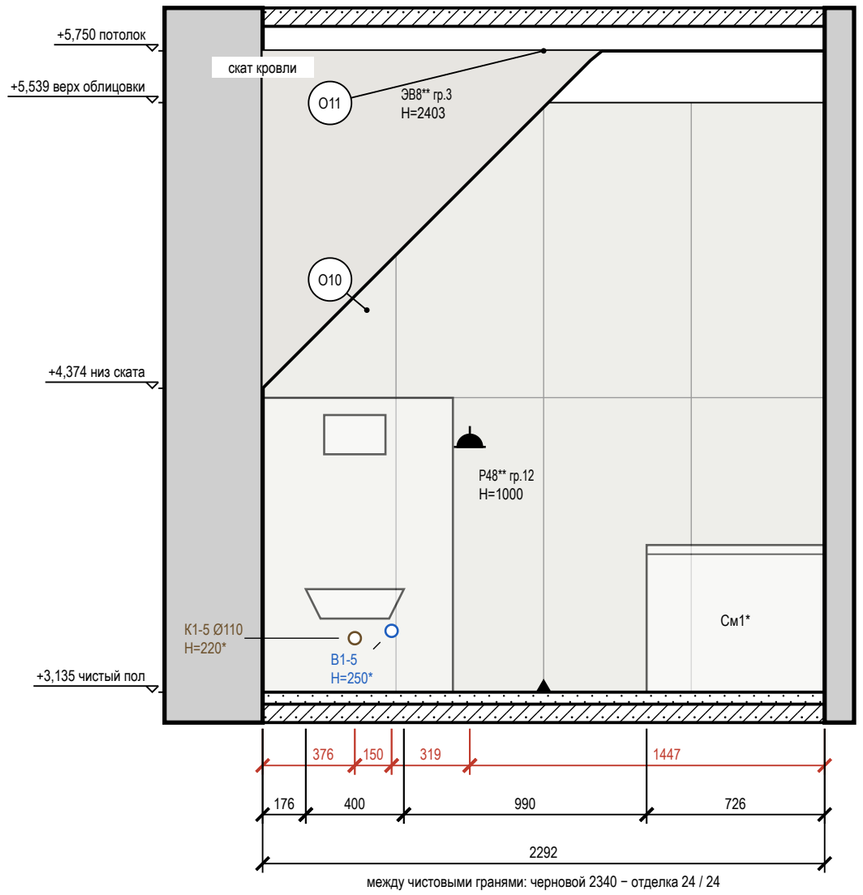

между чистовыми гранями: черновой 2340 − отделка 24 / 24

Схема развёрток (М 1:100)

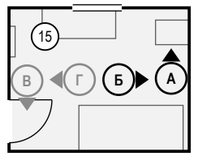

Условные обозначения

- розетка влагозащищённая IP44
- вывод кабеля для подключения прибора (без розетки), марка ЭВ
- вывод В1 (код — в ведомости привязок)
- вывод К1 (код — в ведомости привязок)
- привязки точек и выводов от угла и от пола, мм
- мебель и приборы — фасад по расстановке (условно)
- окно: проём, рама, подоконник
- стены и перекрытия в сечении
- плитка: сетка швов по формату, ▲ — ось старта
- О1 — марка отделки по реестру отделки альбома
- А — марка развёртки: буква стены, стрелка — взгляд

Ведомость отделки (на листе)

Марка	Поверхность	Материал, изделие	Цвет, код	Кол.
О10	стены	облицовка плиткой, Atlas Concorde Marvel Travertine, 600×1200×9 мм, A8UZ, затирка CG2WA	Atlas Concorde A8UZ «Marvel Travertine»	11,8 м²
О11	потолок	окраска, Little Greene Intelligent Bathroom, матовая, подготовка Q3	Little Greene No. 105 «Slaked Lime»	6,9 м²

Примечания

1. Развёртки — вид на стену изнутри помещения, по часовой стрелке; расположение — на схеме листа и на листе 128; размеры — в мм по чистовым поверхностям; отметки — в м от ±0,000 (чистый пол 1-го этажа); высоты Н — от чистого пола помещения до оси изделия, у декора — до центра.
2. Красная цепочка — привязки электроточек и выводов по осям от угла чистовых стен; высота Н — у знака, от чистого пола до оси; высоты мебели, проёмов и границ отделки — колонкой отметок слева. Стена с 5 и более точками или с мелкими звеньями привязок показана двумя видами: архитектурная развёртка (мебель, отделка, проёмы, высоты) и вид «Привязки» на отдельном листе — точки и выводы с марками, одна цепочка по осям и таблица привязок (каждая точка — строка).
3. Стена А показана двумя видами: здесь — архитектурная развёртка (мебель, отделка, проёмы, высоты), электроточки и выводы ВК с привязками и таблицей — на листе 177 («Привязки»).
4. У знака электроточки: марка (Р — розетка, S — выключатель, Св — светильник, ЭВ — вывод кабеля), ×N — число постов в рамке, гр. — группа щита, Н — высота оси от чистого пола, мм; группы по клавишам выключателя — на листе выключателей.
5. Схема мебели, приборов и декора не является технической документацией для производства мебели; габариты — по паспортам изделий (* — высота не задана в проекте, показана по типовому изделию).
6. Выводы ВК — коды и высоты по листу выводов сантехники; * — высота принята по типовой практике монтажа, окончательно — по паспорту прибора.
7. Облицовка — по сетке швов 2 мм, раскладка от оси стены (треугольник у пола), целые ряды от пола; подрезки — по листу раскладки плитки.
8. Гидроизоляция в 2 слоя, заход на стены 200 мм; над ванной — до 2000 и 300 мм за борт — до облицовки, с актом скрытых работ и тестом проливом (узел — на листе узлов).

1000 мм · печать 1:1

Допущения и предложения на листе. Знак «*» принято (замерить): отметка чистого пола этажа «Мансарда» +3,150. Знак «**» предложено (согласовать). См. лист открытых вопросов (листы 8–10).

Изм.	Кол.уч	Лист	№ док.	Подп.	Дата
Разраб.		Кырлан А.С.			04.11.26
Пров.					
ГИП					
Н. контр.					
Утв.					

ГД-2026-010-АИ

Дом 331 м²

Общая площадь 270,67* м² · * размеры приняты, не замерены (реестр — л. 8–10, К-1)

Дизайн-проект интерьера

Стадия	Лист	Листов
РП	175	216

Развёртки стен А, Б. Санузел мастер (пом. 15)

М 1:25

Кырлан Александр Сергеевич


выпуск 04.11.2026 № 2a77323a49 · стр. 179 из 221

Развёртки стен В, Г. Санузел мастер (пом. 15)

Санузел мастер (пом. 15) · вид изнутри помещения · размеры в мм, отметки в м от ±0,000 (чистый пол 1-го этажа)


ПРЕДВАРИТЕЛЬНО · не для производства работ · открыто пунктов: 15 (реестр — л. 8–10)

Развёртка стены В

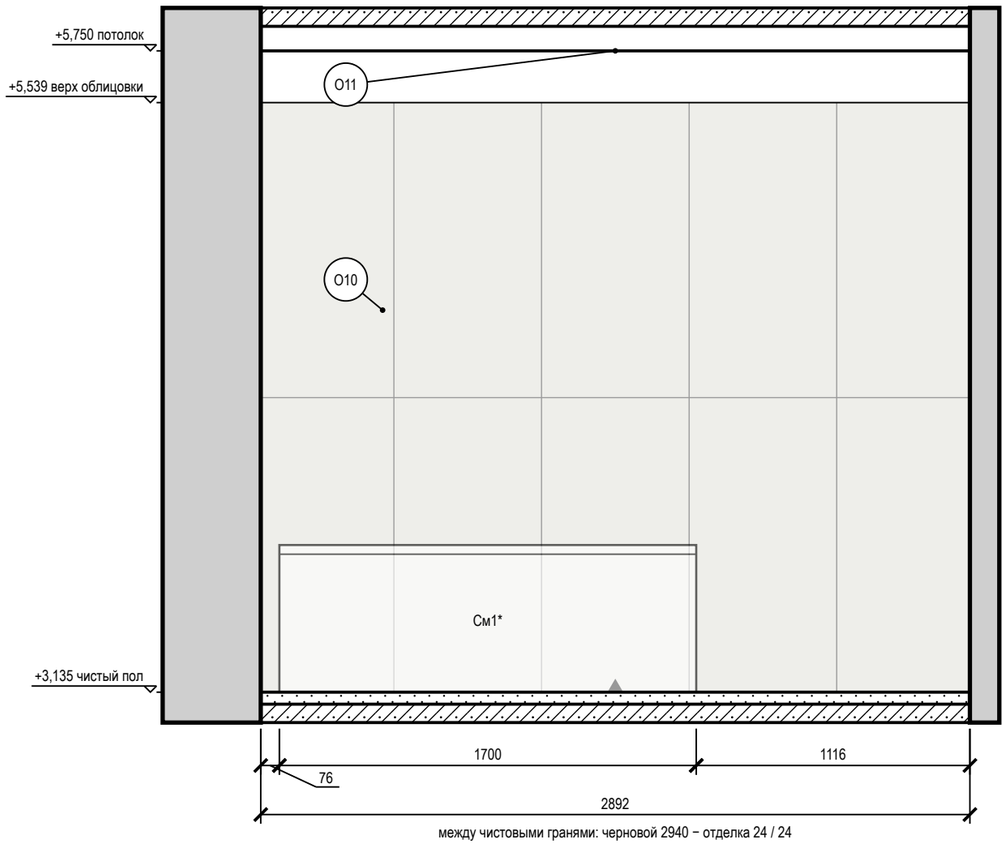


между чистовыми гранями: черновой 2940 − отделка 24 / 24

Развёртка стены Г

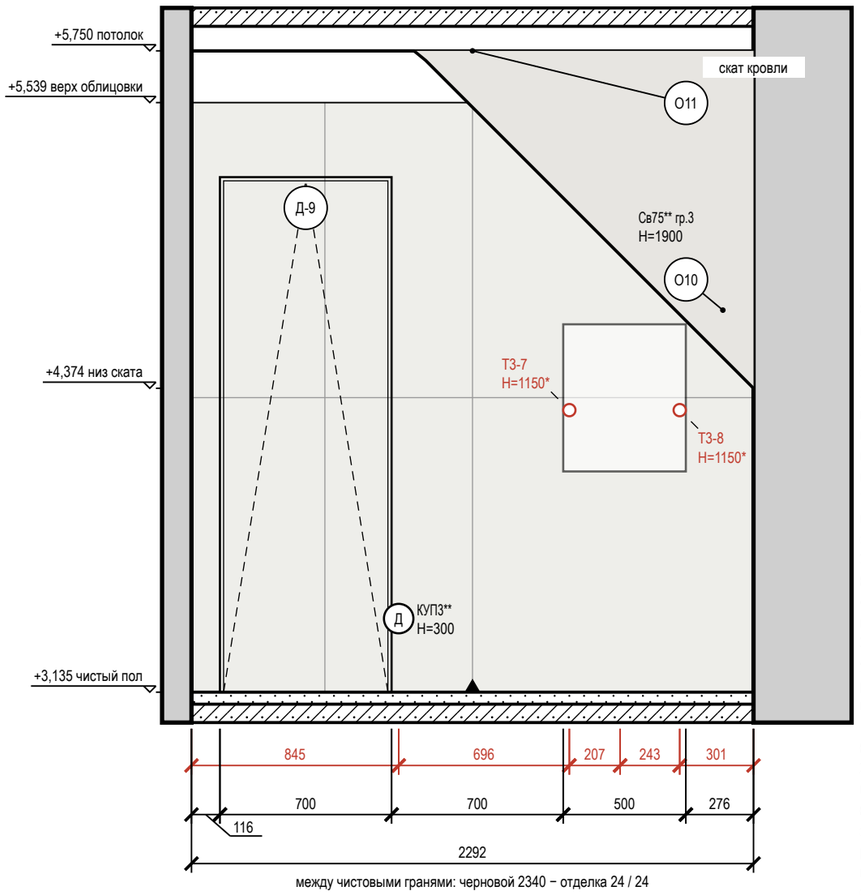

между чистовыми гранями: черновой 2340 − отделка 24 / 24

Схема развёрток (М 1:100)

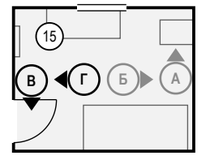

Допущения и предложения на листе

Основа листа: размеры и контуры этажей подобраны проектировщиком по составу помещений и площадям этажей с картинки 470 px (размеры на ней не читаются); обмер и исходный проект — задание (К-1); высоты: 1-й этаж 2800 мм, мансарда 2700 мм (горизонтальная часть) приняты; скаты кровли мансарды приняты по картинке: колено 1200 мм, уклон 45°, конёк вдоль длинной стороны; проект КР — задание (К-2); наружные стены 400 мм, перегородки 120 мм приняты (К-1); разрешённая мощность 15 кВт принята по типовым ТУ для частного дома (К-4); подрайон климата не задан — принят не северный (жилые от 2,5 м) (К-7).

Знак «*» — принято, не замерено и не подтверждено (замерить на объекте): К-2: отметка чистого пола этажа «Мансарда» +3,150 — принята без источника, все отметки мансарды считаются от неё.

Знак «**» — предложение проектировщика, заказчиком не утверждено (согласовать с заказчиком): Св75 — Сдвиг под раскладку плитки стены Г на 32 мм вдоль стены — ось на шве или в центре плитки, привязка по таблице листа; КУП3 — по образцу: Добавлены выводы к вентиляторам: ЭВ4 (ВР1, ванная) и ЭВ5 (ВР3, санузел 2) — группа 3, высота 2389 мм, включение с основным светом, таймер выбега в вентиляторе; и коробки уравнивания потенциалов КУП3 (ванная) и КУП2 (санузел 2) — высота 300 мм, у входа, вне зон 0–2, проводник от шины PE щита ЩК …; сдвиг под раскладку плитки стены Г на 71 мм вдоль стены — ось на шве или в центре плитки, привязка по таблице листа.

См. лист открытых вопросов (лист 8, записи К-1, К-2, К-4, К-7).

Условные обозначения

- светильник настенный (бра), H — высота оси
- вывод Т3 (код — в ведомости привязок)
- привязки точек и выводов от угла и от пола, мм
- мебель и приборы — фасад по расстановке (условно)
- дверь скрытого монтажа: полотно в плоскости стены (узел — на листе узлов)
- стены и перекрытия в сечении
- плитка: сетка швов по формату, ▲ — ось старта
- О1 — марка отделки по реестру отделки альбома
- А — марка развёртки: буква стены, стрелка — взгляд

Ведомость отделки (на листе)

Марка	Поверхность	Материал, изделие	Цвет, код	Кол.
О10	стены	облицовка плиткой, Atlas Concorde Marvel Travertine, 600×1200×9 мм, A8UZ, затирка CG2WA	Atlas Concorde A8UZ «Marvel Travertine»	11 м²
О11	потолок	окраска, Little Greene Intelligent Bathroom, матовая, подготовка Q3	Little Greene No. 105 «Slaked Lime»	6,9 м²

Примечания

1. Развёртки — вид на стену изнутри помещения, по часовой стрелке; расположение — на схеме листа и на листе 128; размеры — в мм по чистовым поверхностям; отметки — в м от ±0,000 (чистый пол 1-го этажа); высоты H — от чистого пола помещения до оси изделия, у декора — до центра.
2. Красная цепочка — привязки электроточек и выводов по осям от угла чистовых стен; высота H — у знака, от чистого пола до оси; высоты мебели, проёмов и границ отделки — колонкой отметок слева. Стена с 5 и более точками или с мелкими звеньями привязок показана двумя видами: архитектурная развёртка (мебель, отделка, проёмы, высоты) и вид «Привязки» на отдельном листе — точки и выводы с марками, одна цепочка по осям и таблица привязок (каждая точка — строка).
3. Стена В показана двумя видами: здесь — архитектурная развёртка (мебель, отделка, проёмы, высоты), электроточки и выводы ВК с привязками и таблицей — на листе 177 («Привязки»).
4. У знака электроточки: марка (Р — розетка, S — выключатель, Св — светильник, ЭВ — вывод кабеля), ×N — число постов в рамке, гр. — группа щита, H — высота оси от чистого пола, мм; группы по клавишам выключателя — на листе выключателей.
5. Схема мебели, приборов и декора не является технической документацией для производства мебели; габариты — по паспортам изделий (* — высота не задана в проекте, показана по типовому изделию).
6. Выводы ВК — коды и высоты по листу выводов сантехники; * — высота принята по типовой практике монтажа, окончательно — по паспорту прибора.
7. Облицовка — по сетке швов 2 мм, раскладка от оси стены (треугольник у пола), целые ряды от пола; подрезки — по листу раскладки плитки.
8. Гидроизоляция в 2 слоя, заход на стены 200 мм; над ванной — до 2000 и 300 мм за борт — до облицовки, с актом скрытых работ и тестом проливом (узел — на листе узлов).
9. Двери скрытого монтажа — полотно в плоскости стены, отделка стены по полотну, плинтус прерывается у короба (узел — на листе узлов).

1000 мм · печать 1:1

Изм.	Кол.уч	Лист	№ док.	Подп.	Дата
Разраб.		Кырлан А.С.			04.11.26
Пров.					
ГИП					
Н. контр.					
Утв.					

ГД-2026-010-АИ

Дом 331 м²

Общая площадь 270,67* м² · * размеры приняты, не замерены (реестр — л. 8–10, К-1)

Дизайн-проект интерьера

Стадия	Лист	Листов
РП	176	216

Развёртки стен В, Г. Санузел мастер (пом. 15)

М 1:25

Кырлан Александр Сергеевич


выпуск 04.11.2026 № 2a77323a49 · стр. 180 из 221

Привязки электроточек и выводов ВК, стены А, В. Санузел мастер (пом. 15)

Санузел мастер (пом. 15) · вид изнутри помещения · привязки в мм, отметки в м · к развёртке на листе 175, 176

ПРЕДВАРИТЕЛЬНО · не для производства работ · открыто пунктов: 15 (реестр — л. 8–10)

Развёртка стены А: электроточки и выводы

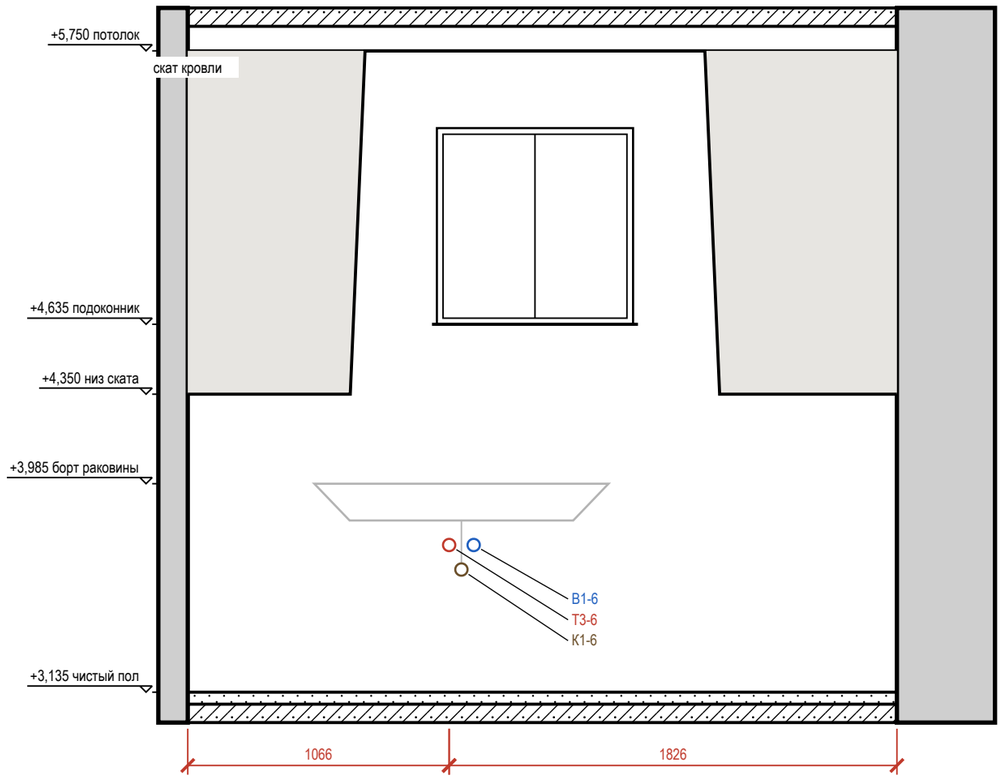

Развёртка стены В: электроточки и выводы

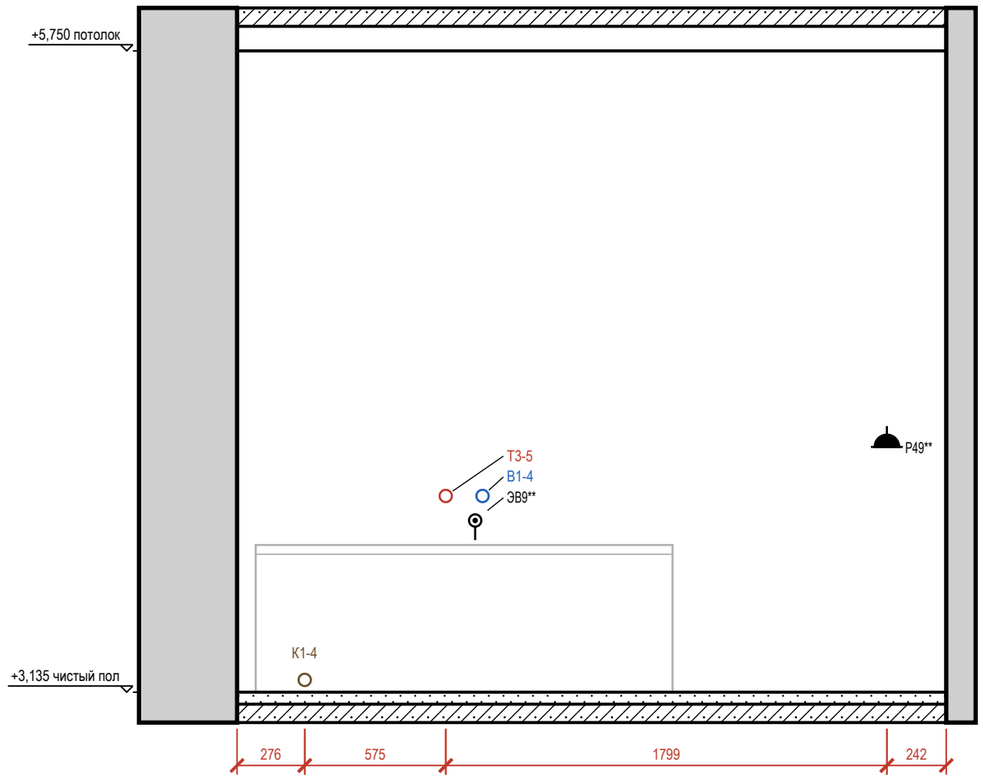


Таблица привязок электроточек и выводов

Стена	Марка	Назначение	От угла, мм	H от пола, мм	Примечание
A	T3-6	горячая вода — умывальник	1066	600*	межос. 100
A	K1-6	канализация — умывальник	1116	500*	Ø50
A	B1-6	холодная вода — умывальник	1166	600*	межос. 100
B	K1-4	канализация — ванна	276	50*	Ø50

Стена	Марка	Назначение	От угла, мм	H от пола, мм	Примечание
B	T3-5	горячая вода — ванна	851	800*	межос. 150
B	ЭВ9**	вывод кабеля: полотенцесушитель П10	971	700	гр. 13
B	B1-4	холодная вода — ванна	1001	800*	межос. 150
B	P49**	розетка: фен у умывальника	2650	1000	гр. 13, IP44

Условные обозначения

- розетка влагозащищённая IP44
- вывод кабеля для подключения прибора (без розетки), марка ЭВ
- вывод B1 (код — в ведомости привязок)
- вывод T3 (код — в ведомости привязок)
- вывод K1 (код — в ведомости привязок)
- привязки точек и выводов от угла и от пола, мм

Примечания

1. Вид «Привязки» стен А, В — электроточки и выводы ВК; архитектурная развёртка (мебель, отделка, проёмы, высоты) — на листах 175, 176, расположение — на листе 128. Мебель и приборы — подложкой для ориентира; их марки и обозначения мебели, проёмов и стен — там же.
2. Привязки — в мм: по горизонтали от левого чистового угла стены до оси изделия, H — от чистого пола до оси; все точки — в таблице привязок. Красная цепочка — привязки по осям; точки ближе 150 мм одна к другой в цепочку не дробятся — их привязки только в таблице.
3. У знака — марка электроточки (P — розетка, S — выключатель, Св — светильник, ЭВ — вывод кабеля); посты в рамке и группа щита — в графе «Примечание»; группы по клавишам выключателя — на листе выключателей.
4. Коды выводов ВК: B1 — холодная вода, T3 — горячая вода, K1 — канализация; номер после дефиса — номер вывода на листе выводов сантехники; * — высота принята по типовой практике монтажа, окончательно — по паспорту прибора.

Допущения и предложения на листе

Основа листа: размеры и контуры этажей подобраны проектировщиком по составу помещений и площадям этажей с картинки 470 px (размеры на ней не читаются); обмер и исходный проект — задание (К-1); высоты: 1-й этаж 2800 мм, мансарда 2700 мм (горизонтальная часть) приняты; скаты кровли мансарды приняты по картинке: колено 1200 мм, уклон 45°, конёк вдоль длинной стороны; проект КР — задание (К-2); наружные стены 400 мм, перегородки 120 мм приняты (К-1); разрешённая мощность 15 кВт принята по типовым ТУ для частного дома (К-4); подрайон климата не задан — принят не северный (жилые от 2,5 м) (К-7).

Знак «*» — принято, не замерено и не подтверждено (замерить на объекте): К-2: отметка чистого пола этажа «Мансарда» +3,150 — принята без источника, все отметки мансарды считаются от неё.

Знак «**» — предложение проектировщика, заказчиком не утверждено (согласовать с заказчиком): ЭВ9 — место и тип котла не выбраны (газ / электро — вопрос заказчику): вывод у стены D, уточнить по проекту котельной; P49 — по образцу: P48, P49 и P33 на высоте 1000 мм — верхний предел нормы (ПУЭ, п. 6.6.30, не выше 1 м); флаг решения снят; сдвиг под раскладку плитки стены В на 26 мм вдоль стены — ось на шве или в центре плитки, привязка по таблице листа.

См. лист открытых вопросов (лист 8, записи К-1, К-2, К-4, К-7).

1000 мм · печать 1:1

Изм.	Кол.уч	Лист	№ док.	Подп.	Дата
Разраб.		Кырлан А.С.			04.11.26
Пров.					
ГИП					
Н. контр.					
Утв.					

ГД-2026-010-АИ

Дом 331 м²

Общая площадь 270,67* м² · * размеры приняты, не замерены (реестр — л. 8–10, К-1)

Дизайн-проект интерьера

Стадия	Лист	Листов
РП	177	216

Привязки электроточек и выводов ВК, стены А, В. Санузел мастер (пом. 15)

М 1:25

Кырлан Александр Сергеевич


выпуск 04.11.2026 № 2a77323a49 · стр. 181 из 221

Развёртка стены А. Спальня 2 (пом. 16)

Спальня 2 (пом. 16) · вид изнутри помещения · размеры в мм, отметки в м от ±0,000 (чистый пол 1-го этажа)


ПРЕДВАРИТЕЛЬНО · не для производства работ · открыто пунктов: 15 (реестр — л. 8–10)

Развёртка стены А

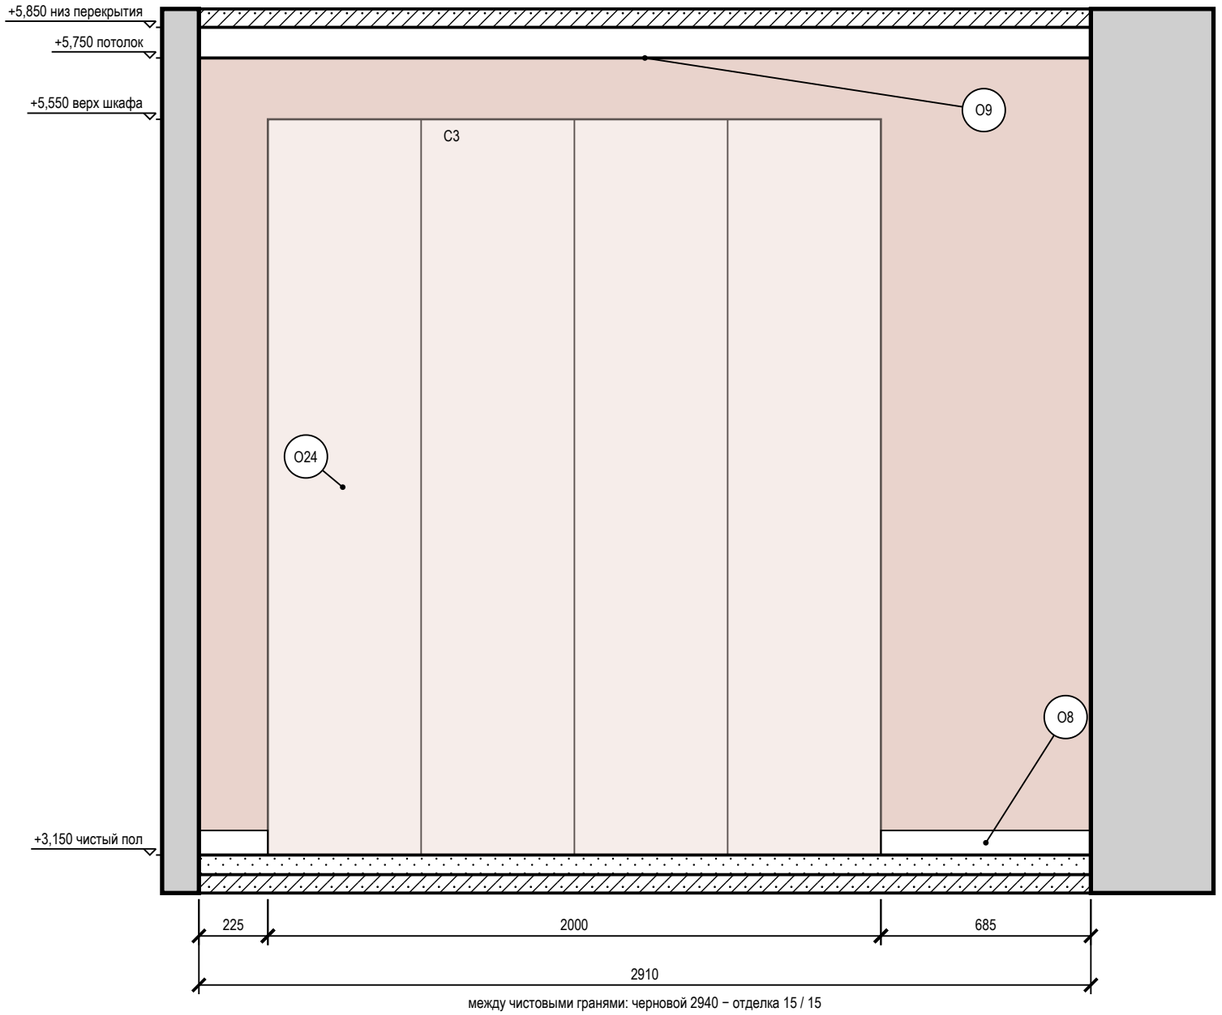

между чистовыми гранями: черновой 2940 − отделка 15 / 15

Схема развёрток (М 1:100)

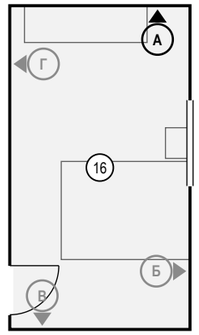

Условные обозначения

- мебель и приборы — фасад по расстановке (условно)
- стены и перекрытия в сечении
- окраска: тон — цвет по коду производителя (условно)
- О1 — марка отделки по реестру отделки альбома
- А — марка развёртки: буква стены, стрелка — взгляд

Ведомость отделки (на листе)

Марка	Поверхность	Материал, изделие	Цвет, код	Кол.
О8	плинтус	плинтус МДФ, h 80 мм, аналог: плинтус МДФ под покраску 80×16	Farrow & Ball No. 226 «Joa's White»	0,9 м
О9	потолок	окраска, Little Greene Absolute Matt, глубокоматовая, подготовка Q3	Little Greene No. 105 «Slaked Lime»	15,5 м²
О24	акцентная стена	окраска, Farrow & Ball Modern Emulsion, матовая, подготовка Q3	Farrow & Ball No. 64 «Red Earth»	7,6 м²

Допущения и предложения на листе

Основа листа: размеры и контуры этажей подобраны проектировщиком по составу помещений и площадям этажей с картинки 470 px (размеры на ней не читаются); обмер и исходный проект — задание (К-1); высоты: 1-й этаж 2800 мм, мансарда 2700 мм (горизонтальная часть) приняты; скаты кровли мансарды приняты по картинке: колено 1200 мм, уклон 45°, конёк вдоль длинной стороны; проект КР — задание (К-2); наружные стены 400 мм, перегородки 120 мм приняты (К-1); разрешённая мощность 15 кВт принята по типовым ТУ для частного дома (К-4); подрайон климата не задан — принят не северный (жилые от 2,5 м) (К-7).

Знак «*» — принято, не замерено и не подтверждено (замерить на объекте): К-2: отметка чистого пола этажа «Мансарда» +3,150 — принята без источника, все отметки мансарды считаются от неё. См. лист открытых вопросов (лист 8, записи К-1, К-2, К-4, К-7).

Примечания

1. Развёртки — вид на стену изнутри помещения, по часовой стрелке; расположение — на схеме листа и на листе 128; размеры — в мм по чистовым поверхностям; отметки — в м от ±0,000 (чистый пол 1-го этажа); высоты Н — от чистого пола помещения до оси изделия, у декора — до центра.
2. Стена А показана двумя видами: здесь — архитектурная развёртка (мебель, отделка, проёмы, высоты), электроточки и выводы ВК с привязками и таблицей — на листе 179 («Привязки»).
3. Схема мебели, приборов и декора не является технической документацией для производства мебели; габариты — по паспортам изделий.
4. Потолок — у каждой стены свой, по плану потолков (ПТ6); ступени — зоной, кромка короба перед нишей — тонкой линией; в поле потолка: ПТ5 +5,650.

1000 мм · печать 1:1

Изм.	Кол.уч	Лист	№ док.	Подп.	Дата
Разраб.		Кырлан А.С.			04.11.26
Пров.					
ГИП					
Н. контр.					
Утв.					

ГД-2026-010-АИ

Дом 331 м²

Общая площадь 270,67* м² · * размеры приняты, не замерены (реестр — л. 8–10, К-1)

Дизайн-проект интерьера

Стадия	Лист	Листов
РП	178	216

Развёртка стены А. Спальня 2 (пом. 16)

М 1:20

Кырлан Александр Сергеевич

выпуск 04.11.2026 № 2a77323a49 · стр. 182 из 221

Привязки электроточек, стена А. Спальня 2 (пом. 16)

Спальня 2 (пом. 16) · вид изнутри помещения · привязки в мм, отметки в м · к развёртке на листе 178

ПРЕДВАРИТЕЛЬНО · не для производства работ · открыто пунктов: 15 (реестр — л. 8–10)

Развёртка стены А: электроточки и выводы

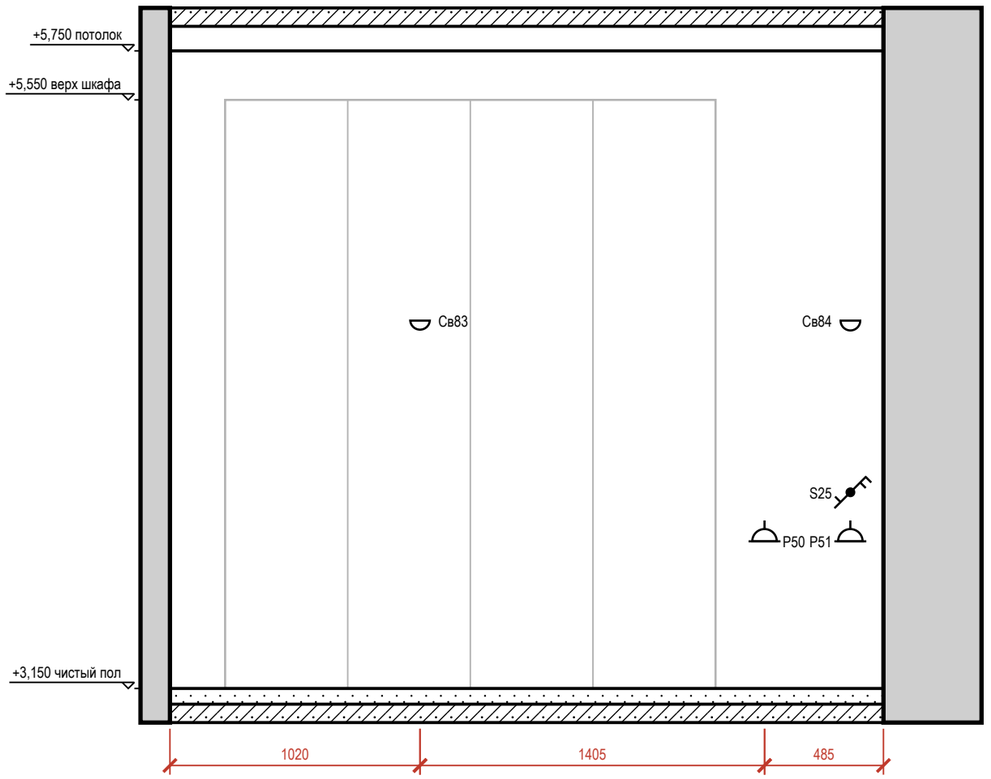



Таблица привязок электроточек и выводов

Марка	Назначение	От угла, мм	Н от пола, мм	Примечание
Св83	светильник настенный	1020	1500	гр. 1
P50	розетка: у кровати	2425	600	гр. 17
P51	розетка: у кровати	2775	600	гр. 17
S25	выключатель	2775	800	гр. 1
Св84	светильник настенный	2775	1500	гр. 1

Условные обозначения

- розетка с заземляющим контактом; у знака — марка, ×N постов в рамке, гр. — группа щита, Н — высота оси, мм
- выключатель одноклавишный
- выключатель двухклавишный (флажков — по числу клавиш)
- выключатель с проходной или перекрёстной клавишей (обратный флажок); тип клавиши — в подписи
- светильник настенный (бра), Н — высота оси
- привязки точек и выводов от угла и от пола, мм
- марка развёртки: буква стены, стрелка — взгляд

Схема развёрток (М 1:100)

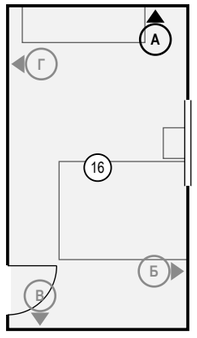

Примечания

1. Вид «Привязки» стены А — электроточки и выводы ВК; архитектурная развёртка (мебель, отделка, проёмы, высоты) — на листе 178, расположение — на листе 128. Мебель и приборы — подложкой для ориентира; их марки и обозначения мебели, проёмов и стен — там же.
2. Привязки — в мм: по горизонтали от левого чистового угла стены до оси изделия, Н — от чистого пола до оси; все точки — в таблице привязок. Красная цепочка — привязки по осям; точки ближе 150 мм одна к другой в цепочку не дробятся — их привязки только в таблице.
3. У знака — марка электроточки (Р — розетка, S — выключатель, Св — светильник, ЭВ — вывод кабеля); посты в рамке и группа щита — в графе «Примечание»; группы по клавишам выключателя — на листе выключателей.

Допущения и предложения на листе

Основа листа: размеры и контуры этажей подобраны проектировщиком по составу помещений и площадям этажей с картинки 470 px (размеры на ней не читаются); обмер и исходный проект — задание (К-1); высоты: 1-й этаж 2800 мм, мансарда 2700 мм (горизонтальная часть) приняты; скаты кровли мансарды приняты по картинке: колено 1200 мм, уклон 45°, конёк вдоль длинной стороны; проект КР — задание (К-2); наружные стены 400 мм, перегородки 120 мм приняты (К-1); разрешённая мощность 15 кВт принята по типовым ТУ для частного дома (К-4); подрайон климата не задан — принят не северный (жилые от 2,5 м) (К-7).

Знак «*» — принято, не замерено и не подтверждено (замерить на объекте): К-2: отметка чистого пола этажа «Мансарда» +3,150 — принята без источника, все отметки мансарды считаются от неё.

См. лист открытых вопросов (лист 8, записи К-1, К-2, К-4, К-7).

1000 мм · печать 1:1

Изм.	Кол.уч	Лист	№ док.	Подп.	Дата
Разраб.		Кырлан А.С.			04.11.26
Пров.					
ГИП					
Н. контр.					
Утв.					

ГД-2026-010-АИ

Дом 331 м²

Общая площадь 270,67* м² · * размеры приняты, не замерены (реестр — л. 8–10, К-1)

Дизайн-проект интерьера	Стадия	Лист	Листов
	РП	179	216

Привязки электроточек, стена А. Спальня 2 (пом. 16)

М 1:25

Кырлан Александр Сергеевич


выпуск 04.11.2026 № 2a77323a49 · стр. 183 из 221

Развёртка стены Б. Спальня 2 (пом. 16)

Спальня 2 (пом. 16) · вид изнутри помещения · размеры в мм, отметки в м от ±0,000 (чистый пол 1-го этажа)


ПРЕДВАРИТЕЛЬНО · не для производства работ · открыто пунктов: 15 (реестр — л. 8–10)

Развёртка стены Б

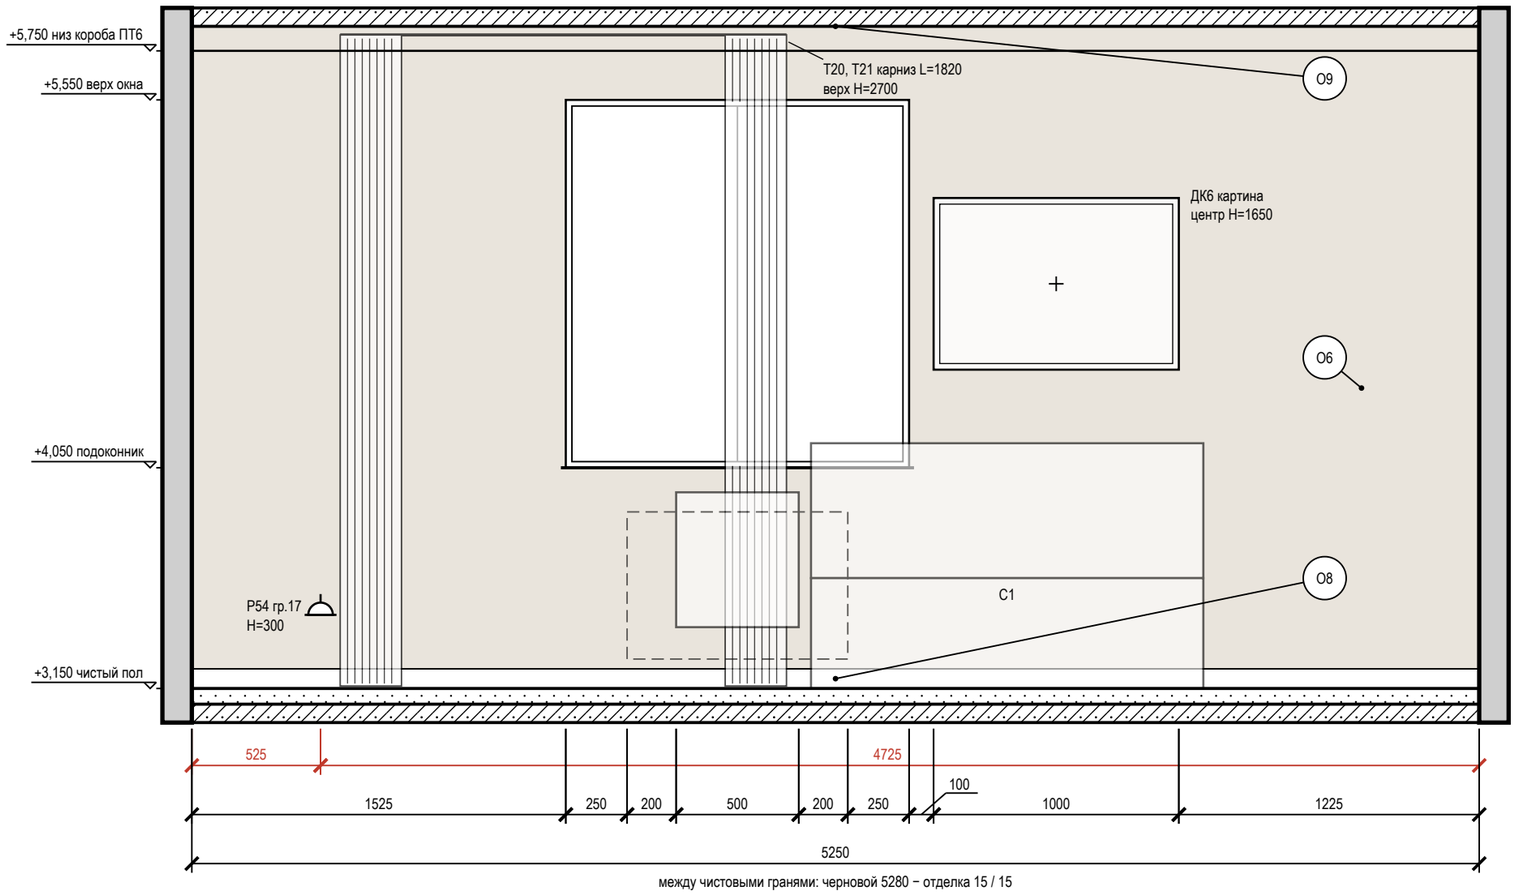

между чистовыми гранями: черновой 5280 − отделка 15 / 15

Схема развёрток (М 1:100)

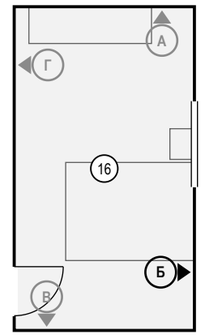

Условные обозначения

- розетка с заземляющим контактом; у знака — марка, ×N постов в рамке, гр. — группа щита, Н — высота оси, мм
- привязки точек и выводов от угла и от пола, мм
- мебель и приборы — фасад по расстановке (условно)
- картина (декор): марка Д, крест — центр, Н — высота центра, мм
- карниз (шина) и шторы в собранном виде: марка Т, длина L, верх Н
- окно: проём, рама, подоконник
- радиатор отопления; марка — по плану отопления
- стены и перекрытия в сечении
- окраска: тон — цвет по коду производителя (условно)
- О1 — марка отделки по реестру отделки альбома
- А — марка развёртки: буква стены, стрелка — взгляд

Ведомость отделки (на листе)

Марка	Поверхность	Материал, изделие	Цвет, код	Кол.
О6	стены	окраска, Farrow & Ball Modern Emulsion, матовая, подготовка Q3	Farrow & Ball No. 226 «Joa's White»	12,1 м²
О8	плинтус	плинтус МДФ, h 80 мм, аналог: плинтус МДФ под покраску 80×16	Farrow & Ball No. 226 «Joa's White»	5,3 м
О9	потолок	окраска, Little Greene Absolute Matt, глубокоматовая, подготовка Q3	Little Greene No. 105 «Slaked Lime»	15,5 м²

Примечания

1. Развёртки — вид на стену изнутри помещения, по часовой стрелке; расположение — на схеме листа и на листе 128; размеры — в мм по чистовым поверхностям; отметки — в м от ±0,000 (чистый пол 1-го этажа); высоты Н — от чистого пола помещения до оси изделия, у декора — до центра.
2. Красная цепочка — привязки электроточек и выводов по осям от угла чистовых стен; высота Н — у знака, от чистого пола до оси; высоты мебели, проёмов и границ отделки — колонкой отметок слева. Стена с 5 и более точками или с мелкими звеньями привязок показана двумя видами: архитектурная развёртка (мебель, отделка, проёмы, высоты) и вид «Привязки» на отдельном листе — точки и выводы с марками, одна цепочка по осям и таблица привязок (каждая точка — строка).
3. У знака электроточки: марка (Р — розетка, S — выключатель, Св — светильник, ЭВ — вывод кабеля), ×N — число постов в рамке, гр. — группа щита, Н — высота оси от чистого пола, мм; группы по клавишам выключателя — на листе выключателей.
4. Схема мебели, приборов и декора не является технической документацией для производства мебели; габариты — по паспортам изделий.
5. Картины и зеркала крепить к основанию по паспорту изделия (закладные и анкеры — в перечне скрытых работ); крест — ось центра предмета.
6. Карнизы (шины) — по ведомости текстиля декоратора: длина L и верх Н на развёртке — те же числа, что в ведомости; крепление — до окраски потолка.
7. Потолок — у каждой стены свой, по плану потолков (НШ3, ПТ6); ступени — зоной, кромка короба перед нишей — тонкой линией; в поле потолка: ПТ5 +5,650.
8. Линии узора (швы плитки, складки штор, рёбра радиаторов) прерываются у знаков и выносок — просвет между линиями не менее 0,7 мм.

1000 мм · печать 1:1

Допущения и предложения на листе

Основа листа: размеры и контуры этажей подобраны проектировщиком по составу помещений и площадям этажей с картинки 470 px (размеры на ней не читаются); обмер и исходный проект — задание (К-1); высоты: 1-й этаж 2800 мм, мансарда 2700 мм (горизонтальная часть) приняты; скаты кровли мансарды приняты по картинке: колено 1200 мм, уклон 45°, конёк вдоль длинной стороны; проект КР — задание (К-2); наружные стены 400 мм, перегородки 120 мм приняты (К-1); разрешённая мощность 15 кВт принята по типовым ТУ для частного дома (К-4); подрайон климата не задан — принят не северный (жилые от 2,5 м) (К-7).

Знак «*» — принято, не замерено и не подтверждено (замерить на объекте): К-2: отметка чистого пола этажа «Мансарда» +3,150 — принята без источника, все отметки мансарды считаются от неё.

См. лист открытых вопросов (лист 8, записи К-1, К-2, К-4, К-7).

Изм.	Кол.уч	Лист	№ док.	Подп.	Дата
Разраб.		Кырлан А.С.			04.11.26
Пров.					
ГИП					
Н. контр.					
Утв.					

ГД-2026-010-АИ

Дом 331 м²

Общая площадь 270,67* м² · * размеры приняты, не замерены (реестр — л. 8–10, К-1)

Дизайн-проект интерьера

Стадия	Лист	Листов
РП	180	216

Развёртка стены Б. Спальня 2 (пом. 16)

М 1:25

Кырлан Александр Сергеевич

выпуск 04.11.2026 № 2a77323a49 · стр. 184 из 221

Развёртка стены В. Спальня 2 (пом. 16)

Спальня 2 (пом. 16) · вид изнутри помещения · размеры в мм, отметки в м от ±0,000 (чистый пол 1-го этажа)

Развёртка стены В


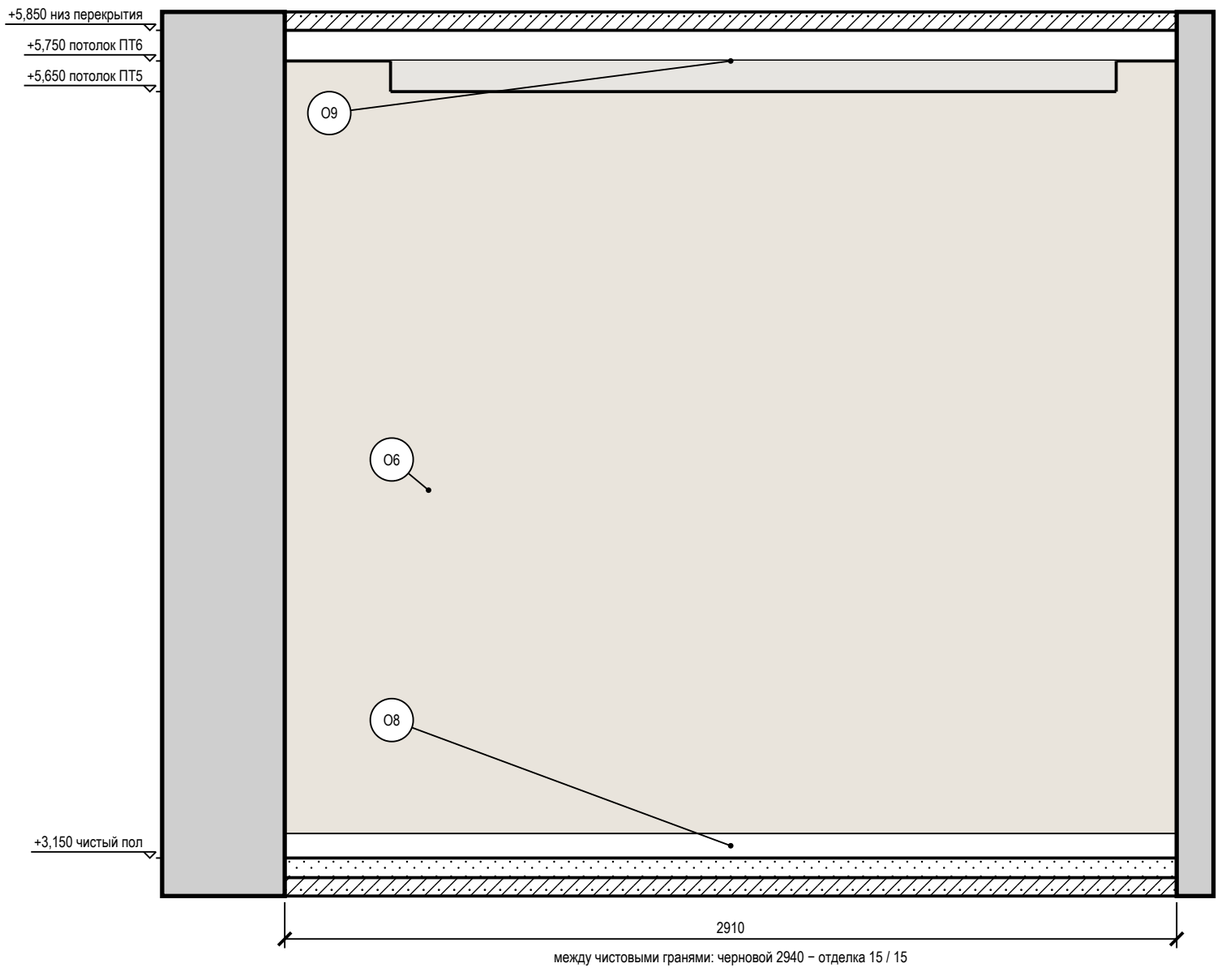


Схема развёрток (М 1:100)

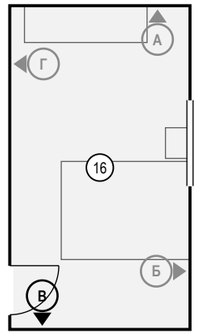

Условные обозначения

- мебель и приборы — фасад по расстановке (условно)
- стены и перекрытия в сечении
- окраска: тон — цвет по коду производителя (условно)
- О1 — марка отделки по реестру отделки альбома
- А — марка развёртки: буква стены, стрелка — взгляд

Ведомость отделки (на листе)

Марка	Поверхность	Материал, изделие	Цвет, код	Кол.
О6	стены	окраска, Farrow & Ball Modern Emulsion, матовая, подготовка Q3	Farrow & Ball No. 226 «Joa's White»	7,6 м²
О8	плинтус	плинтус МДФ, h 80 мм, аналог: плинтус МДФ под покраску 80×16	Farrow & Ball No. 226 «Joa's White»	2,9 м
О9	потолок	окраска, Little Greene Absolute Matt, глубокоматовая, подготовка Q3	Little Greene No. 105 «Slaked Lime»	15,5 м²

Допущения и предложения на листе

Основа листа: размеры и контуры этажей подобраны проектировщиком по составу помещений и площадям этажей с картинки 470 px (размеры на ней не читаются); обмер и исходный проект — задание (К-1); высоты: 1-й этаж 2800 мм, мансарда 2700 мм (горизонтальная часть) приняты; скаты кровли мансарды приняты по картинке: колено 1200 мм, уклон 45°, конёк вдоль длинной стороны; проект КР — задание (К-2); наружные стены 400 мм, перегородки 120 мм приняты (К-1); разрешённая мощность 15 кВт принята по типовым ТУ для частного дома (К-4); подрайон климата не задан — принят не северный (жилые от 2,5 м) (К-7).

Знак «*» — принято, не замерено и не подтверждено (замерить на объекте): К-2: отметка чистого пола этажа «Мансарда» +3,150 — принята без источника, все отметки мансарды считаются от неё. См. лист открытых вопросов (лист 8, записи К-1, К-2, К-4, К-7).

Примечания

1. Развёртки — вид на стену изнутри помещения, по часовой стрелке; расположение — на схеме листа и на листе 128; размеры — в мм по чистовым поверхностям; отметки — в м от ±0,000 (чистый пол 1-го этажа); высоты Н — от чистого пола помещения до оси изделия, у декора — до центра.
2. Стена В показана двумя видами: здесь — архитектурная развёртка (мебель, отделка, проёмы, высоты), электроточки и выводы ВК с привязками и таблицей — на листе 182 («Привязки»).
3. Схема мебели, приборов и декора не является технической документацией для производства мебели; габариты — по паспортам изделий.
4. Потолок — у каждой стены свой, по плану потолков (ПТ6, ПТ5); ступени — зоной, кромка короба перед нишей — тонкой линией.

1000 мм · печать 1:1

Изм.	Кол.уч	Лист	№ док.	Подп.	Дата
Разраб.		Кырлан А.С.			04.11.26
Пров.					
ГИП					
Н. контр.					
Утв.					

ГД-2026-010-АИ

Дом 331 м²

Общая площадь 270,67* м² · * размеры приняты, не замерены (реестр — л. 8–10, К-1)

Дизайн-проект интерьера

Стадия	Лист	Листов
РП	181	216

Развёртка стены В. Спальня 2 (пом. 16)

М 1:20

Кырлан Александр Сергеевич

выпуск 04.11.2026 № 2a77323a49 · стр. 185 из 221

Привязки электроточек, стена В. Спальня 2 (пом. 16)

Спальня 2 (пом. 16) · вид изнутри помещения · привязки в мм, отметки в м · к развёртке на листе 181

ПРЕДВАРИТЕЛЬНО · не для производства работ · открыто пунктов: 15 (реестр — л. 8–10)

Развёртка стены В: электроточки и выводы

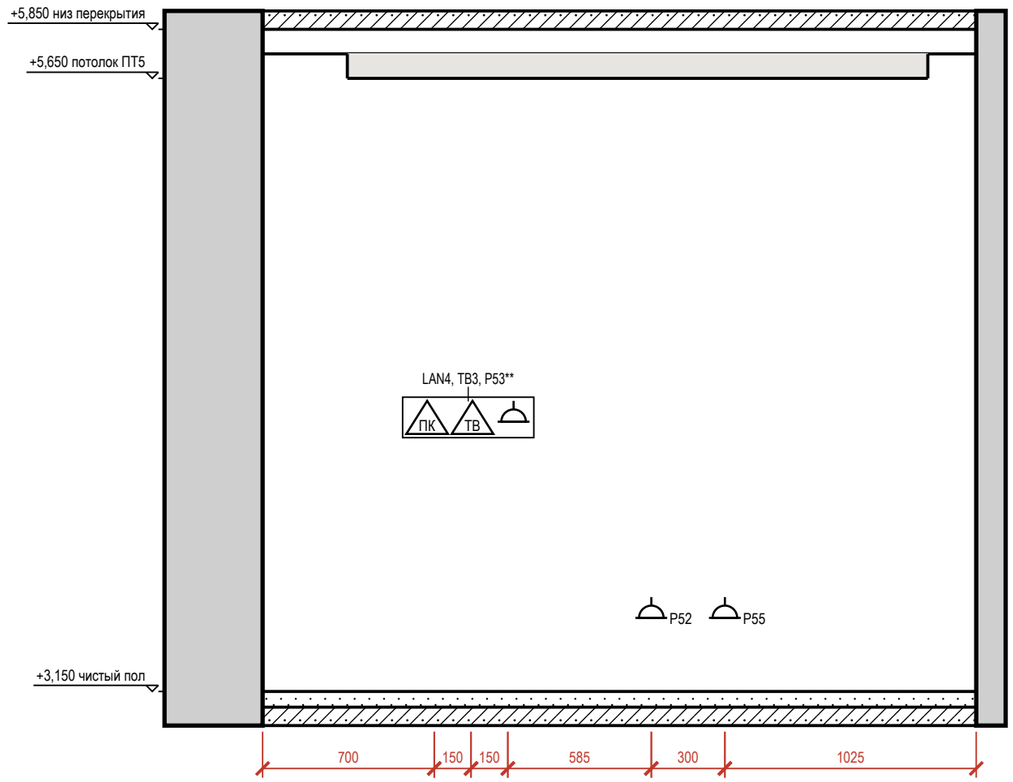



Таблица привязок электроточек и выводов

Марка	Назначение	От угла, мм	Н от пола, мм	Примечание
LAN4	розетка RJ45: Smart TV	700	1100	
ТВ3	розетка ТВ: ТВ над комодом	850	1100	
Р53**	розетка: ТВ над комодом (в одной зоне с ТВ3, LAN4)	1000	1100	гр. 17
Р52	розетка: у комода	1585	300	гр. 17
Р55	розетка: уборка у входа	1885	300	гр. 17

Условные обозначения

- розетка с заземляющим контактом; у знака — марка, ×N постов в рамке, гр. — группа щита, Н — высота оси, мм
- ПК — розетка компьютерная RJ45
- ТВ — розетка телевизионная
- привязки точек и выводов от угла и от пола, мм
- А — марка развёртки: буква стены, стрелка — взгляд

Схема развёрток (М 1:100)

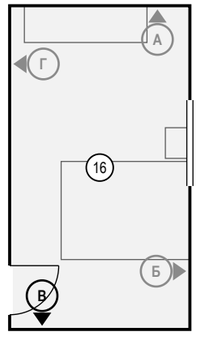

Примечания

1. Вид «Привязки» стены В — электроточки и выводы ВК; архитектурная развёртка (мебель, отделка, проёмы, высоты) — на листе 181, расположение — на листе 128. Мебель и приборы — подложкой для ориентира; их марки и обозначения мебели, проёмов и стен — там же.
2. Привязки — в мм: по горизонтали от левого чистового угла стены до оси изделия, Н — от чистого пола до оси; все точки — в таблице привязок. Красная цепочка — привязки по осям; точки ближе 150 мм одна к другой в цепочку не дробятся — их привязки только в таблице.
3. У знака — марка электроточки (Р — розетка, S — выключатель, Св — светильник, ЭВ — вывод кабеля); посты в рамке и группа щита — в графе «Примечание»; группы по клавишам выключателя — на листе выключателей.

Допущения и предложения на листе

Основа листа: размеры и контуры этажей подобраны проектировщиком по составу помещений и площадям этажей с картинки 470 px (размеры на ней не читаются); обмер и исходный проект — задание (К-1); высоты: 1-й этаж 2800 мм, мансарда 2700 мм (горизонтальная часть) приняты; скаты кровли мансарды приняты по картинке: колено 1200 мм, уклон 45°, конёк вдоль длинной стороны; проект КР — задание (К-2); наружные стены 400 мм, перегородки 120 мм приняты (К-1); разрешённая мощность 15 кВт принята по типовым ТУ для частного дома (К-4); подрайон климата не задан — принят не северный (жилые от 2,5 м) (К-7).

Знак «*» — принято, не замерено и не подтверждено (замерить на объекте): К-2: отметка чистого пола этажа «Мансарда» +3,150 — принята без источника, все отметки мансарды считаются от неё.

Знак «**» — предложение проектировщика, заказчиком не утверждено (согласовать с заказчиком): Р53 — высота 1100 мм выше нормы 1 м (ПУЭ 6.6.30) по назначению: питание ТВ над комодом, в одной зоне с выводами ТВ3 и LAN4.

См. лист открытых вопросов (лист 8, записи К-1, К-2, К-4, К-7).

1000 мм · печать 1:1

Изм.	Кол.уч	Лист	№ док.	Подп.	Дата
Разраб.		Кырлан А.С.			04.11.26
Пров.					
ГИП					
Н. контр.					
Утв.					

ГД-2026-010-АИ

Дом 331 м²

Общая площадь 270,67* м² · * размеры приняты, не замерены (реестр — л. 8–10, К-1)

Дизайн-проект интерьера

Стадия	Лист	Листов
РП	182	216

Привязки электроточек, стена В. Спальня 2 (пом. 16)

М 1:25

Кырлан Александр Сергеевич


выпуск 04.11.2026 № 2a77323a49 · стр. 186 из 221

Развёртка стены Г. Спальня 2 (пом. 16)

Спальня 2 (пом. 16) · вид изнутри помещения · размеры в мм, отметки в м от ±0,000 (чистый пол 1-го этажа)


ПРЕДВАРИТЕЛЬНО · не для производства работ · открыто пунктов: 15 (реестр — л. 8–10)

Развёртка стены Г

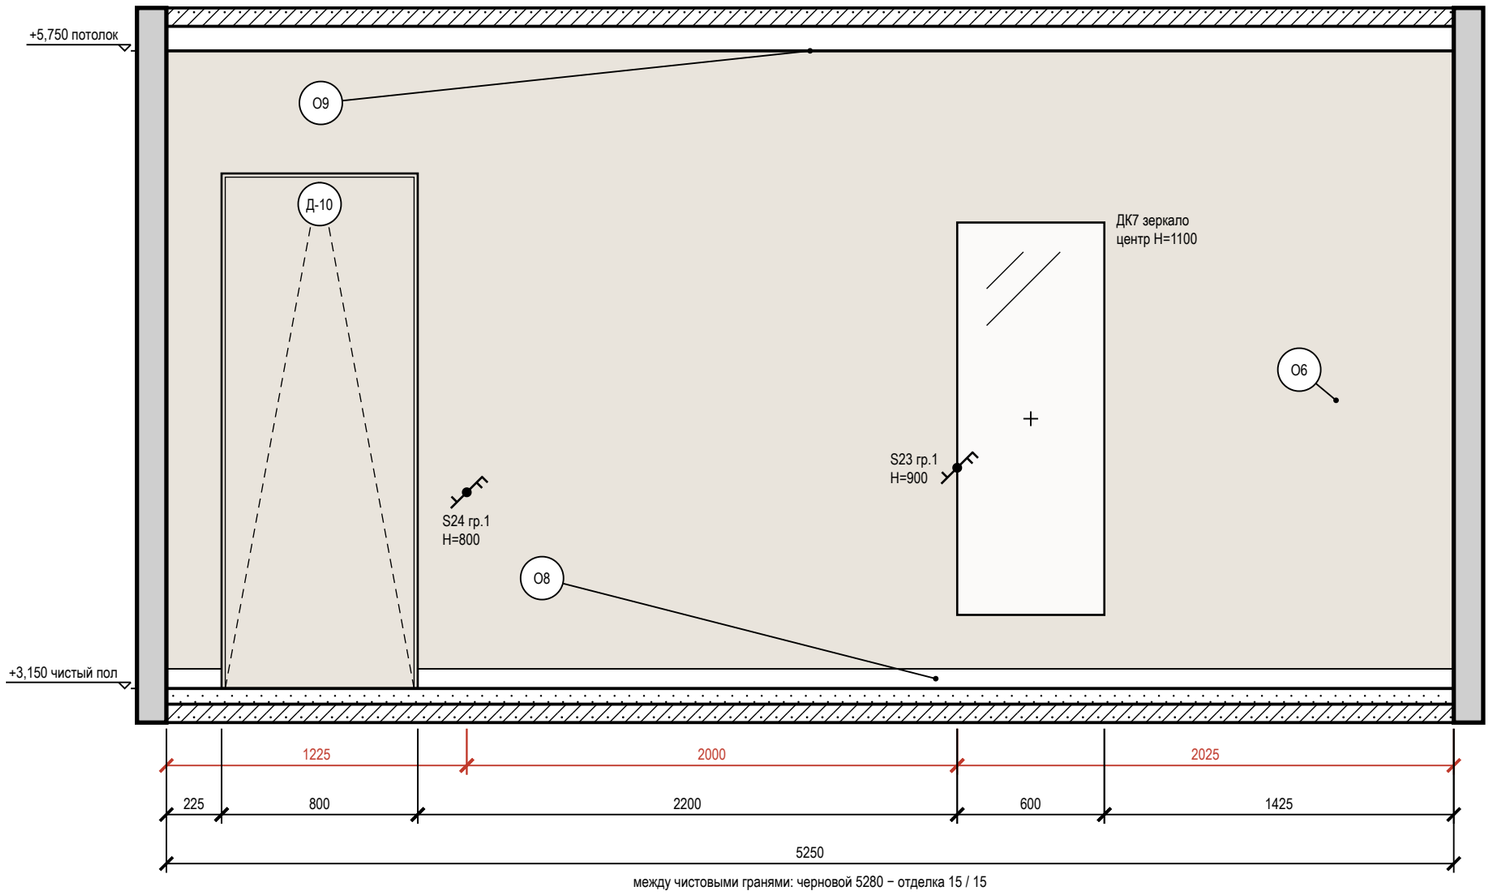

между чистовыми гранями: черновой 5280 − отделка 15 / 15

Схема развёрток (М 1:100)

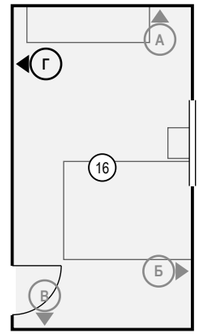

Условные обозначения

- выключатель одноклавишный
- выключатель двухклавишный (флажков — по числу клавиш)
- выключатель с проходной или перекрёстной клавишей (обратный флажок); тип клавиши — в подписи
- привязки точек и выводов от угла и от пола, мм
- мебель и приборы — фасад по расстановке (условно)
- зеркало: марка Д, крест — центр, Н — высота центра, мм
- дверь скрытого монтажа: полотно в плоскости стены (узел — на листе узлов)
- стены и перекрытия в сечении
- окраска: тон — цвет по коду производителя (условно)
- О1 — марка отделки по реестру отделки альбома
- А — марка развёртки: буква стены, стрелка — взгляд

Ведомость отделки (на листе)

Марка	Поверхность	Материал, изделие	Цвет, код	Кол.
О6	стены	окраска, Farrow & Ball Modern Emulsion, матовая, подготовка Q3	Farrow & Ball No. 226 «Joa's White»	12 м²
О8	плинтус	плинтус МДФ, h 80 мм, аналог: плинтус МДФ под покраску 80×16	Farrow & Ball No. 226 «Joa's White»	4,5 м
О9	потолок	окраска, Little Greene Absolute Matt, глубокоматовая, подготовка Q3	Little Greene No. 105 «Slaked Lime»	15,5 м²

Примечания

1. Развёртки — вид на стену изнутри помещения, по часовой стрелке; расположение — на схеме листа и на листе 128; размеры — в мм по чистовым поверхностям; отметки — в м от ±0,000 (чистый пол 1-го этажа); высоты Н — от чистого пола помещения до оси изделия, у декора — до центра.
2. Красная цепочка — привязки электроточек и выводов по осям от угла чистовых стен; высота Н — у знака, от чистого пола до оси; высоты мебели, проёмов и границ отделки — колонкой отметок слева. Стена с 5 и более точками или с мелкими звеньями привязок показана двумя видами: архитектурная развёртка (мебель, отделка, проёмы, высоты) и вид «Привязки» на отдельном листе — точки и выводы с марками, одна цепочка по осям и таблица привязок (каждая точка — строка).
3. У знака электроточки: марка (Р — розетка, S — выключатель, Св — светильник, ЭВ — вывод кабеля), ×N — число постов в рамке, гр. — группа щита, Н — высота оси от чистого пола, мм; группы по клавишам выключателя — на листе выключателей.
4. Схема мебели, приборов и декора не является технической документацией для производства мебели; габариты — по паспортам изделий.
5. Картины и зеркала крепить к основанию по паспорту изделия (закладные и анкеры — в перечне скрытых работ); крест — ось центра предмета.
6. Двери скрытого монтажа — полотно в плоскости стены, отделка стены по полотну, плинтус прерывается у короба (узел — на листе узлов).
7. Потолок — у каждой стены свой, по плану потолков (ПТ6); ступени — зоной, кромка короба перед нишей — тонкой линией; в поле потолка: ПТ5 +5,650.

1000 мм · печать 1:1

Допущения и предложения на листе

Основа листа: размеры и контуры этажей подобраны проектировщиком по составу помещений и площадям этажей с картинки 470 px (размеры на ней не читаются); обмер и исходный проект — задание (К-1); высоты: 1-й этаж 2800 мм, мансарда 2700 мм (горизонтальная часть) приняты; скаты кровли мансарды приняты по картинке: колено 1200 мм, уклон 45°, конёк вдоль длинной стороны; проект КР — задание (К-2); наружные стены 400 мм, перегородки 120 мм приняты (К-1); разрешённая мощность 15 кВт принята по типовым ТУ для частного дома (К-4); подрайон климата не задан — принят не северный (жилые от 2,5 м) (К-7).

Знак «*» — принято, не замерено и не подтверждено (замерить на объекте): К-2: отметка чистого пола этажа «Мансарда» +3,150 — принята без источника, все отметки мансарды считаются от неё.

См. лист открытых вопросов (лист 8, записи К-1, К-2, К-4, К-7).

Изм.	Кол.уч	Лист	№ док.	Подп.	Дата
Разраб.		Кырлан А.С.			04.11.26
Пров.					
ГИП					
Н. контр.					
Утв.					

ГД-2026-010-АИ

Дом 331 м²

Общая площадь 270,67* м² · * размеры приняты, не замерены (реестр — л. 8–10, К-1)

Дизайн-проект интерьера

Стадия	Лист	Листов
РП	183	216

Развёртка стены Г. Спальня 2 (пом. 16)

М 1:25

Кырлан Александр Сергеевич


выпуск 04.11.2026 № 2a77323a49 · стр. 187 из 221

Развёртка стены А. Холл мансарды (пом. 17)

Холл мансарды (пом. 17) · вид изнутри помещения · размеры в мм, отметки в м от ±0,000 (чистый пол 1-го этажа)


ПРЕДВАРИТЕЛЬНО · не для производства работ · открыто пунктов: 15 (реестр — л. 8–10)

Развёртка стены А

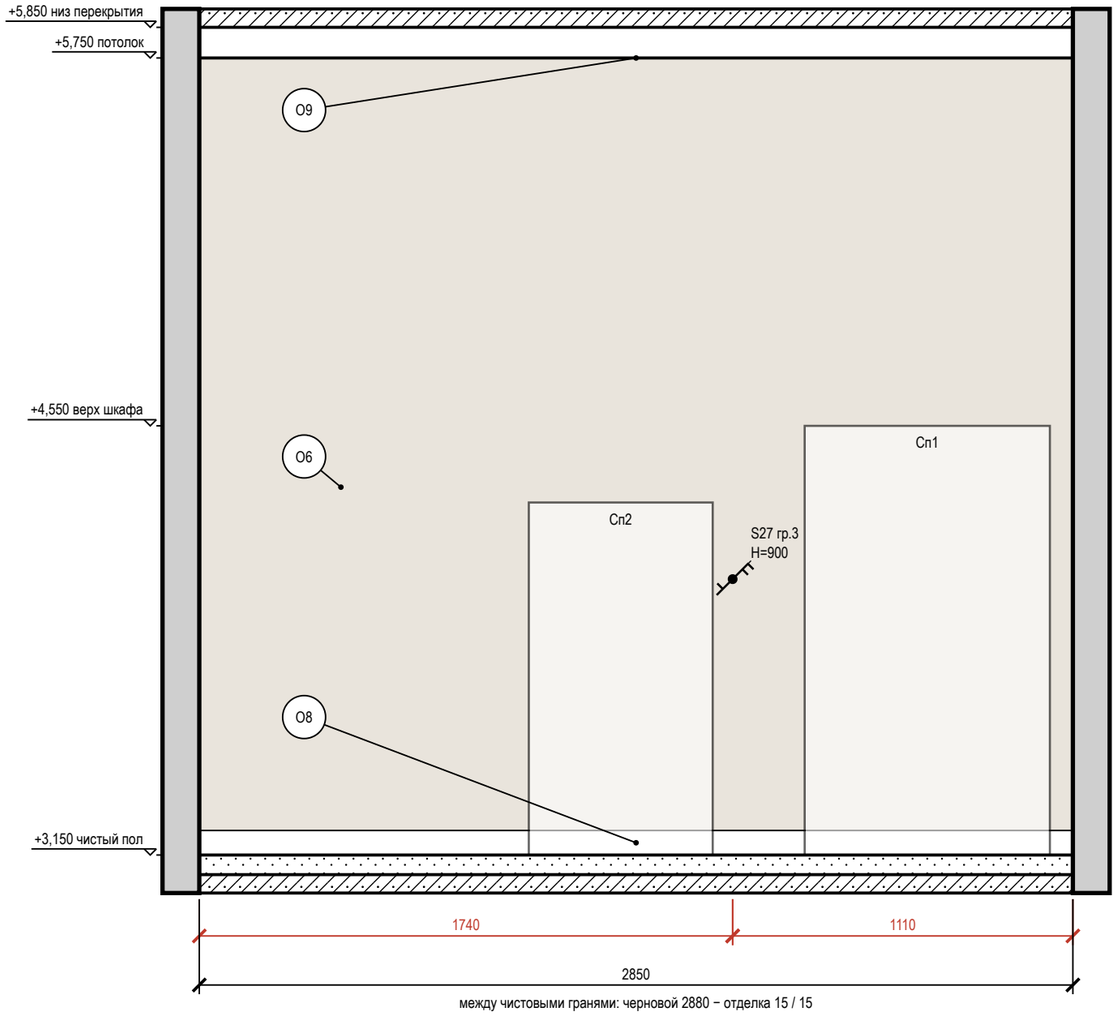

между чистовыми гранями: черновой 2880 − отделка 15 / 15

Схема развёрток (М 1:100)

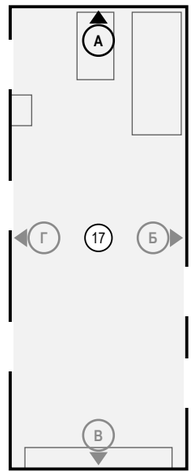

Условные обозначения

- выключатель одноклавишный
- выключатель двухклавишный (флажков — по числу клавиш)
- выключатель с проходной или перекрёстной клавишей (обратный флажок); тип клавиши — в подписи
- привязки точек и выводов от угла и от пола, мм
- мебель и приборы — фасад по расстановке (условно)
- стены и перекрытия в сечении
- окраска: тон — цвет по коду производителя (условно)
- О1 — марка отделки по реестру отделки альбома
- А — марка развёртки: буква стены, стрелка — взгляд

Ведомость отделки (на листе)

Марка	Поверхность	Материал, изделие	Цвет, код	Кол.
О6	стены	окраска, Farrow & Ball Modern Emulsion, матовая, подготовка Q3	Farrow & Ball No. 226 «Joa's White»	7,4 м²
О8	плинтус	плинтус МДФ, h 80 мм, аналог: плинтус МДФ под покраску 80×16	Farrow & Ball No. 226 «Joa's White»	2,9 м
О9	потолок	окраска, Little Greene Absolute Matt, глубокоматовая, подготовка Q3	Little Greene No. 105 «Slaked Lime»	21,7 м²

Допущения и предложения на листе

Основа листа: размеры и контуры этажей подобраны проектировщиком по составу помещений и площадям этажей с картинки 470 px (размеры на ней не читаются); обмер и исходный проект — задание (К-1); высоты: 1-й этаж 2800 мм, мансарда 2700 мм (горизонтальная часть) приняты; скаты кровли мансарды приняты по картинке: колено 1200 мм, уклон 45°, конёк вдоль длинной стороны; проект КР — задание (К-2); наружные стены 400 мм, перегородки 120 мм приняты (К-1); разрешённая мощность 15 кВт принята по типовым ТУ для частного дома (К-4); подрайон климата не задан — принят не северный (жилые от 2,5 м) (К-7).

Знак «*» — принято, не замерено и не подтверждено (замерить на объекте): К-2: отметка чистого пола этажа «Мансарда» +3,150 — принята без источника, все отметки мансарды считаются от неё. См. лист открытых вопросов (лист 8, записи К-1, К-2, К-4, К-7).

Примечания

1. Развёртки — вид на стену изнутри помещения, по часовой стрелке; расположение — на схеме листа и на листе 128; размеры — в мм по чистовым поверхностям; отметки — в м от ±0,000 (чистый пол 1-го этажа); высоты Н — от чистого пола помещения до оси изделия, у декора — до центра.
2. Красная цепочка — привязки электроточек и выводов по осям от угла чистовых стен; высота Н — у знака, от чистого пола до оси; высоты мебели, проёмов и границ отделки — колонкой отметок слева. Стена с 5 и более точками или с мелкими звеньями привязок показана двумя видами: архитектурная развёртка (мебель, отделка, проёмы, высоты) и вид «Привязки» на отдельном листе — точки и выводы с марками, одна цепочка по осям и таблица привязок (каждая точка — строка).
3. У знака электроточки: марка (Р — розетка, S — выключатель, Св — светильник, ЭВ — вывод кабеля), ×N — число постов в рамке, гр. — группа щита, Н — высота оси от чистого пола, мм; группы по клавишам выключателя — на листе выключателей.
4. Схема мебели, приборов и декора не является технической документацией для производства мебели; габариты — по паспортам изделий.

1000 мм · печать 1:1

Изм.	Кол.уч	Лист	№ док.	Подп.	Дата
Разраб.		Кырлан А.С.			04.11.26
Пров.					
ГИП					
Н. контр.					
Утв.					

ГД-2026-010-АИ

Дом 331 м²

Общая площадь 270,67* м² · * размеры приняты, не замерены (реестр — л. 8–10, К-1)

Дизайн-проект интерьера

Стадия	Лист	Листов
РП	184	216

Развёртка стены А. Холл мансарды (пом. 17)

М 1:20

Кырлан Александр Сергеевич


выпуск 04.11.2026 № 2a77323a49 · стр. 188 из 221

Развёртка стены Б. Холл мансарды (пом. 17)

Холл мансарды (пом. 17) · вид изнутри помещения · размеры в мм, отметки в м от ±0,000 (чистый пол 1-го этажа)

ПРЕДВАРИТЕЛЬНО · не для производства работ · открыто пунктов: 15 (реестр — л. 8–10)

Развёртка стены Б

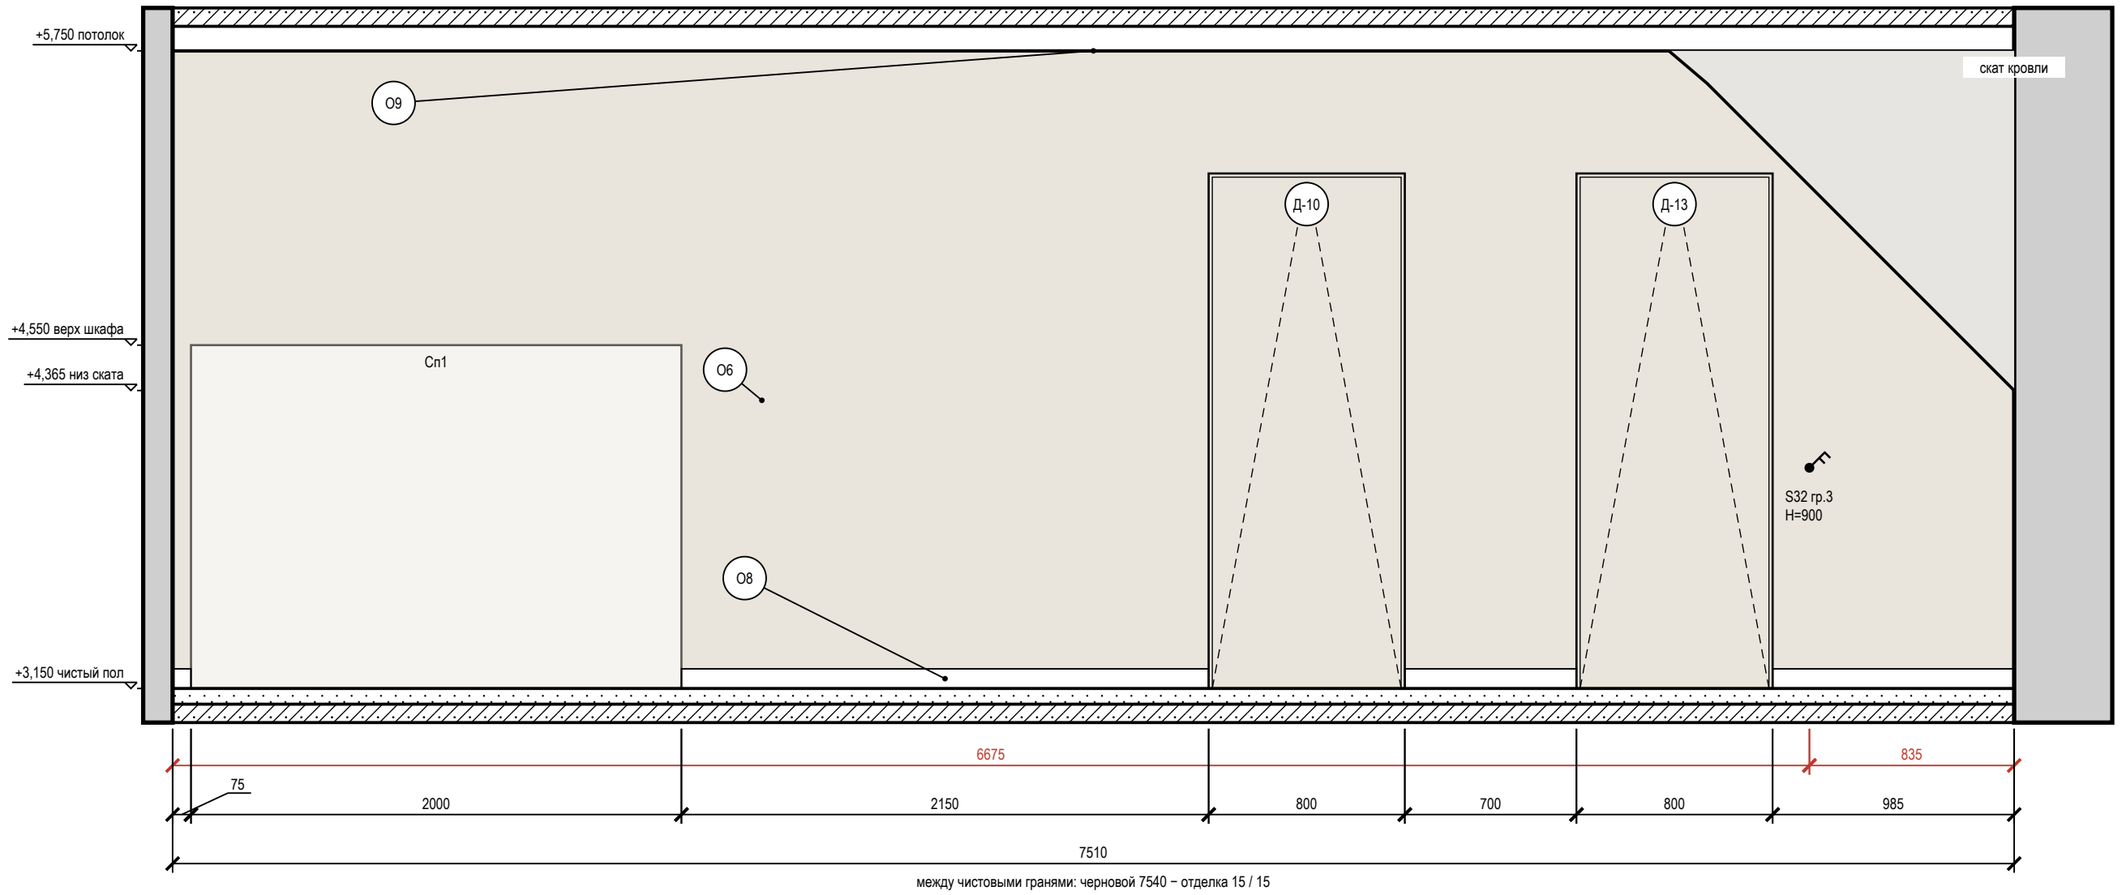

между чистовыми гранями: черновой 7540 − отделка 15 / 15

Условные обозначения

обозначения этого вида, схема развёрток помещения и ведомость отделки — на листе 186

Допущения и предложения на листе

Основа листа: размеры и контуры этажей подобраны проектировщиком по составу помещений и площадям этажей с картинки 470 px (размеры на ней не читаются); обмер и исходный проект — задание (К-1); высоты: 1-й этаж 2800 мм, мансарда 2700 мм (горизонтальная часть) приняты; скаты кровли мансарды приняты по картинке: колено 1200 мм, уклон 45°, конёк вдоль длинной стороны; проект КР — задание (К-2); наружные стены 400 мм, перегородки 120 мм приняты (К-1); разрешённая мощность 15 кВт принята по типовым ТУ для частного дома (К-4); подрайон климата не задан — принят не северный (жилые от 2,5 м) (К-7).

Знак «*» — принято, не замерено и не подтверждено (замерить на объекте): К-2: отметка чистого пола этажа «Мансарда» +3,150 — принята без источника, все отметки мансарды считаются от неё. См. лист открытых вопросов (лист 8, записи К-1, К-2, К-4, К-7).

Примечания

1. Развёртки — вид на стену изнутри помещения, по часовой стрелке; расположение — на схеме листа 186 и на листе 128; размеры — в мм по чистовым поверхностям; отметки — в м от ±0,000 (чистый пол 1-го этажа); высоты Н — от чистого пола помещения до оси изделия, у декора — до центра.
2. Красная цепочка — привязки электроточек и выводов по осям от угла чистовых стен; высота Н — у знака, от чистого пола до оси; высоты мебели, проёмов и границ отделки — колонкой отметок слева. Стена с 5 и более точками или с мелкими звеньями привязок показана двумя видами: архитектурная развёртка (мебель, отделка, проёмы, высоты) и вид «Привязки» на отдельном листе — точки и выводы с марками, одна цепочка по осям и таблица привязок (каждая точка — строка).
3. У знака электроточки: марка (Р — розетка, S — выключатель, Св — светильник, ЭВ — вывод кабеля), ×N — число постов в рамке, гр. — группа щита, Н — высота оси от чистого пола, мм; группы по клавишам выключателя — на листе выключателей.
4. Схема мебели, приборов и декора не является технической документацией для производства мебели; габариты — по паспортам изделий.
5. Двери скрытого монтажа — полотно в плоскости стены, отделка стены по полотну, плинтус прерывается у короба (узел — на листе узлов).

1000 мм · печать 1:1

Изм.	Кол.уч	Лист	№ док.	Подп.	Дата
Разраб.		Кырлан А.С.			04.11.26
Пров.					
ГИП					
Н. контр.					
Утв.					

ГД-2026-010-АИ

Дом 331 м²

Общая площадь 270,67* м² · * размеры приняты, не замерены (реестр — л. 8–10, К-1)

Дизайн-проект интерьера

Стадия	Лист	Листов
РП	185	216

Развёртка стены Б. Холл мансарды (пом. 17)

М 1:25


Кырлан Александр Сергеевич

выпуск 04.11.2026 № 2a77323a49 · стр. 189 из 221

Развёртка стены Б: схема и ведомость отделки. Холл мансарды (пом. 17)

Холл мансарды (пом. 17) · к развёртке на листе 185

Схема развёрток (М 1:50)

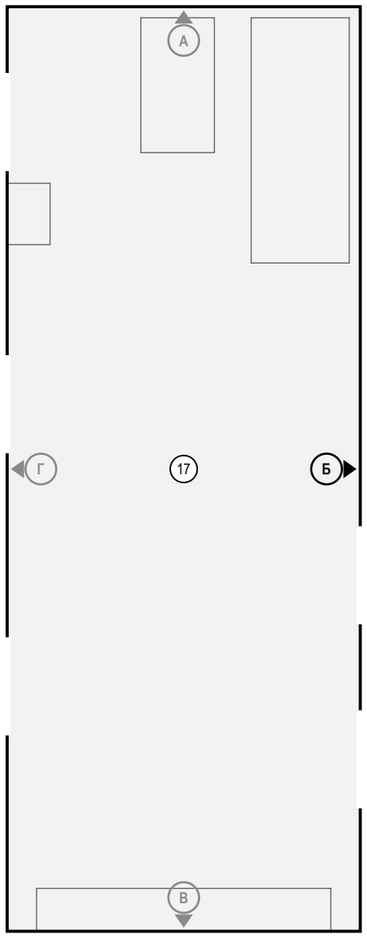

Условные обозначения

- выключатель одноклавишный
- выключатель двухклавишный (флажков — по числу клавиш)
- привязки точек и выводов от угла и от пола, мм
- мебель и приборы — фасад по расстановке (условно)
- дверь скрытого монтажа: полотно в плоскости стены (узел — на листе узлов)
- стены и перекрытия в сечении
- окраска: тон — цвет по коду производителя (условно)
- О1 — марка отделки по реестру отделки альбома
- А — марка развёртки: буква стены, стрелка — взгляд

Ведомость отделки (на листе)

Марка	Поверхность	Материал, изделие	Цвет, код	Кол.
О6	стены	окраска, Farrow & Ball Modern Emulsion, матовая, подготовка Q3	Farrow & Ball No. 226 «Joa's White»	16,2 м²
О8	плинтус	плинтус МДФ, h 80 мм, аналог: плинтус МДФ под покраску 80×16	Farrow & Ball No. 226 «Joa's White»	3,9 м
О9	потолок	окраска, Little Greene Absolute Matt, глубокоматовая, подготовка Q3	Little Greene No. 105 «Slaked Lime»	21,7 м²

Примечания

1. Схема, условные обозначения и ведомость отделки — к развёртке стены Б на листе 185: вид в своём масштабе занимает лист целиком.
2. Расположение развёрток всех помещений — на листе 128; полная ведомость отделки — на листах отделочника.

Допущения и предложения на листе

Основа листа: размеры и контуры этажей подобраны проектировщиком по составу помещений и площадям этажей с картинки 470 px (размеры на ней не читаются); обмер и исходный проект — задание (К-1); высоты: 1-й этаж 2800 мм, мансарда 2700 мм (горизонтальная часть) приняты; скаты кровли мансарды приняты по картинке: колено 1200 мм, уклон 45°, конёк вдоль длинной стороны; проект КР — задание (К-2); наружные стены 400 мм, перегородки 120 мм приняты (К-1); разрешённая мощность 15 кВт принята по типовым ТУ для частного дома (К-4); подрайон климата не задан — принят не северный (жилые от 2,5 м) (К-7).

Знак «*» — принято, не замерено и не подтверждено (замерить на объекте): К-2: отметка чистого пола этажа «Мансарда» +3,150 — принята без источника, все отметки мансарды считаются от неё.

Знак «**» — предложение проектировщика, заказчиком не утверждено (согласовать с заказчиком): плинтус пом. 17 — артикул изделия не выбран: позиция описана характеристиками («аналог по характеристикам»), артикул выбирается при закупке.

См. лист открытых вопросов (лист 8, записи К-1, К-2, К-4, К-7).

Изм.	Кол.уч	Лист	№ док.	Подп.	Дата
Разраб.		Кырлан А.С.			04.11.26
Пров.					
ГИП					
Н. контр.					
Утв.					

ГД-2026-010-АИ

Дом 331 м²

Общая площадь 270,67* м² · * размеры приняты, не замерены (реестр — л. 8–10, К-1)

Дизайн-проект интерьера

Стадия	Лист	Листов
РП	186	216

Развёртка стены Б: схема и ведомость отделки. Холл мансарды (пом. 17)

М б/м

Кырлан Александр Сергеевич


выпуск 04.11.2026 № 2a77323a49 · стр. 190 из 221

Развёртка стены В. Холл мансарды (пом. 17)

Холл мансарды (пом. 17) · вид изнутри помещения · размеры в мм, отметки в м от ±0,000 (чистый пол 1-го этажа)


ПРЕДВАРИТЕЛЬНО · не для производства работ · открыто пунктов: 15 (реестр — л. 8–10)

Развёртка стены В

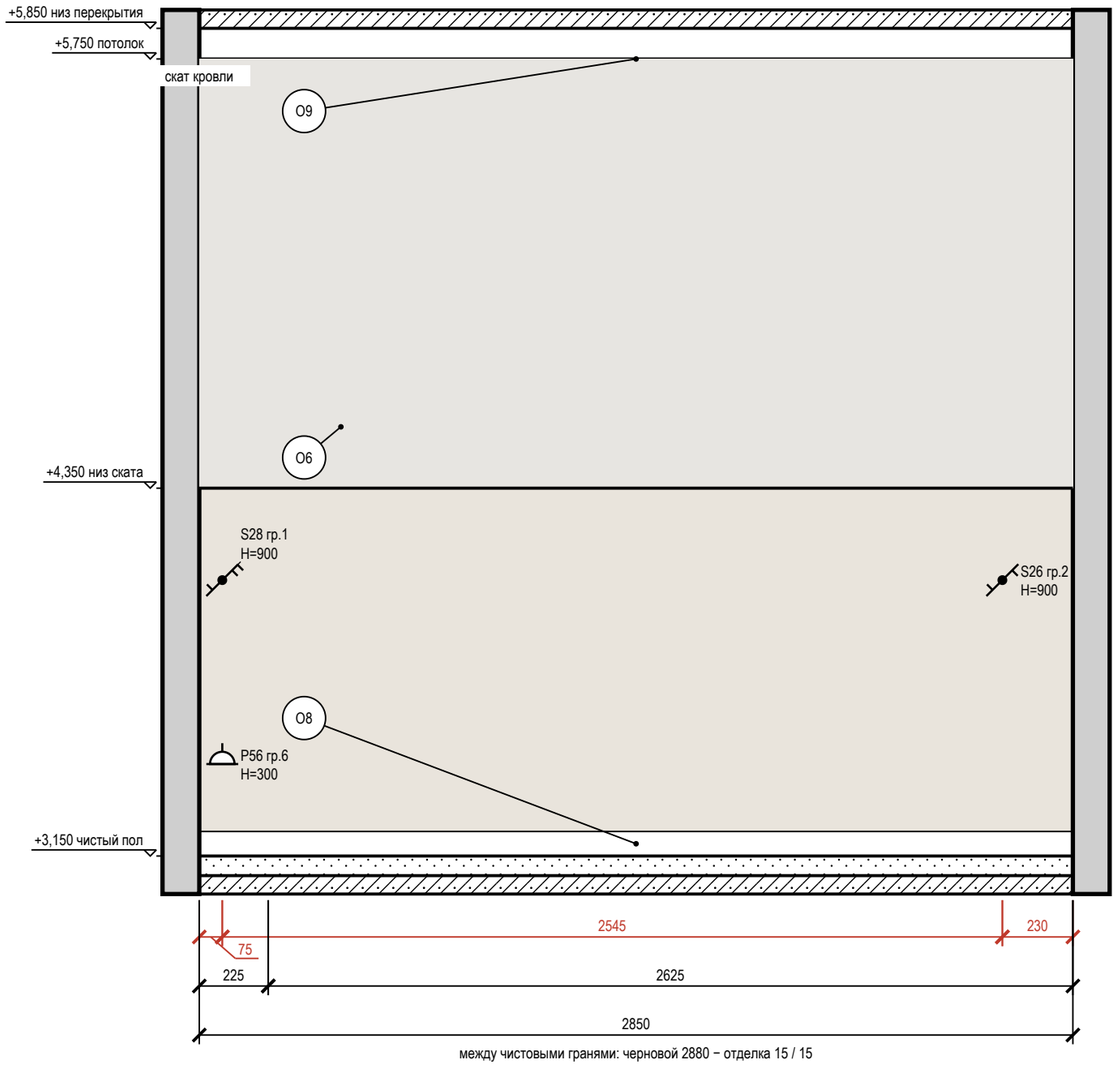

между чистовыми гранями: черновой 2880 − отделка 15 / 15

Схема развёрток (М 1:100)

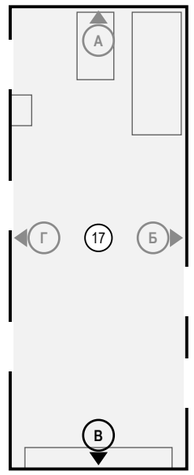

Условные обозначения

- розетка с заземляющим контактом; у знака — марка, ×N постов в рамке, гр. — группа щита, Н — высота оси, мм
- выключатель одноклавишный
- выключатель двухклавишный (флажков — по числу клавиш)
- выключатель с проходной или перекрёстной клавишей (обратный флажок); тип клавиши — в подписи
- привязки точек и выводов от угла и от пола, мм
- мебель и приборы — фасад по расстановке (условно)
- стены и перекрытия в сечении
- окраска: тон — цвет по коду производителя (условно)
- О1 — марка отделки по реестру отделки альбома
- А — марка развёртки: буква стены, стрелка — взгляд

Ведомость отделки (на листе)

Марка	Поверхность	Материал, изделие	Цвет, код	Кол.
О6	стены	окраска, Farrow & Ball Modern Emulsion, матовая, подготовка Q3	Farrow & Ball No. 226 «Joa's White»	7,4 м²
О8	плинтус	плинтус МДФ, h 80 мм, аналог: плинтус МДФ под покраску 80×16	Farrow & Ball No. 226 «Joa's White»	2,9 м
О9	потолок	окраска, Little Greene Absolute Matt, глубокоматовая, подготовка Q3	Little Greene No. 105 «Slaked Lime»	21,7 м²

Допущения и предложения на листе

Основа листа: размеры и контуры этажей подобраны проектировщиком по составу помещений и площадям этажей с картинки 470 px (размеры на ней не читаются); обмер и исходный проект — задание (К-1); высоты: 1-й этаж 2800 мм, мансарда 2700 мм (горизонтальная часть) приняты; скаты кровли мансарды приняты по картинке: колено 1200 мм, уклон 45°, конёк вдоль длинной стороны; проект КР — задание (К-2); наружные стены 400 мм, перегородки 120 мм приняты (К-1); разрешённая мощность 15 кВт принята по типовым ТУ для частного дома (К-4); подрайон климата не задан — принят не северный (жилые от 2,5 м) (К-7).

Знак «*» — принято, не замерено и не подтверждено (замерить на объекте): К-2: отметка чистого пола этажа «Мансарда» +3,150 — принята без источника, все отметки мансарды считаются от неё. См. лист открытых вопросов (лист 8, записи К-1, К-2, К-4, К-7).

Примечания

1. Развёртки — вид на стену изнутри помещения, по часовой стрелке; расположение — на схеме листа и на листе 128; размеры — в мм по чистовым поверхностям; отметки — в м от ±0,000 (чистый пол 1-го этажа); высоты Н — от чистого пола помещения до оси изделия, у декора — до центра.
2. Красная цепочка — привязки электроточек и выводов по осям от угла чистовых стен; высота Н — у знака, от чистого пола до оси; высоты мебели, проёмов и границ отделки — колонкой отметок слева. Стена с 5 и более точками или с мелкими звеньями привязок показана двумя видами: архитектурная развёртка (мебель, отделка, проёмы, высоты) и вид «Привязки» на отдельном листе — точки и выводы с марками, одна цепочка по осям и таблица привязок (каждая точка — строка).
3. У знака электроточки: марка (Р — розетка, S — выключатель, Св — светильник, ЭВ — вывод кабеля), ×N — число постов в рамке, гр. — группа щита, Н — высота оси от чистого пола, мм; группы по клавишам выключателя — на листе выключателей.
4. Схема мебели, приборов и декора не является технической документацией для производства мебели; габариты — по паспортам изделий (* — высота не задана в проекте, показана по типовому изделию).

1000 мм · печать 1:1

Изм.	Кол.уч	Лист	№ док.	Подп.	Дата
Разраб.		Кырлан А.С.			04.11.26
Пров.					
ГИП					
Н. контр.					
Утв.					

ГД-2026-010-АИ

Дом 331 м²

Общая площадь 270,67* м² · * размеры приняты, не замерены (реестр — л. 8–10, К-1)

Дизайн-проект интерьера

Стадия	Лист	Листов
РП	187	216

Развёртка стены В. Холл мансарды (пом. 17)

М 1:20

Кырлан Александр Сергеевич


выпуск 04.11.2026 № 2a77323a49 · стр. 191 из 221

Развёртка стены Г. Холл мансарды (пом. 17)

Холл мансарды (пом. 17) · вид изнутри помещения · размеры в мм, отметки в м от ±0,000 (чистый пол 1-го этажа)

ПРЕДВАРИТЕЛЬНО · не для производства работ · открыто пунктов: 15 (реестр — л. 8–10)

Развёртка стены Г

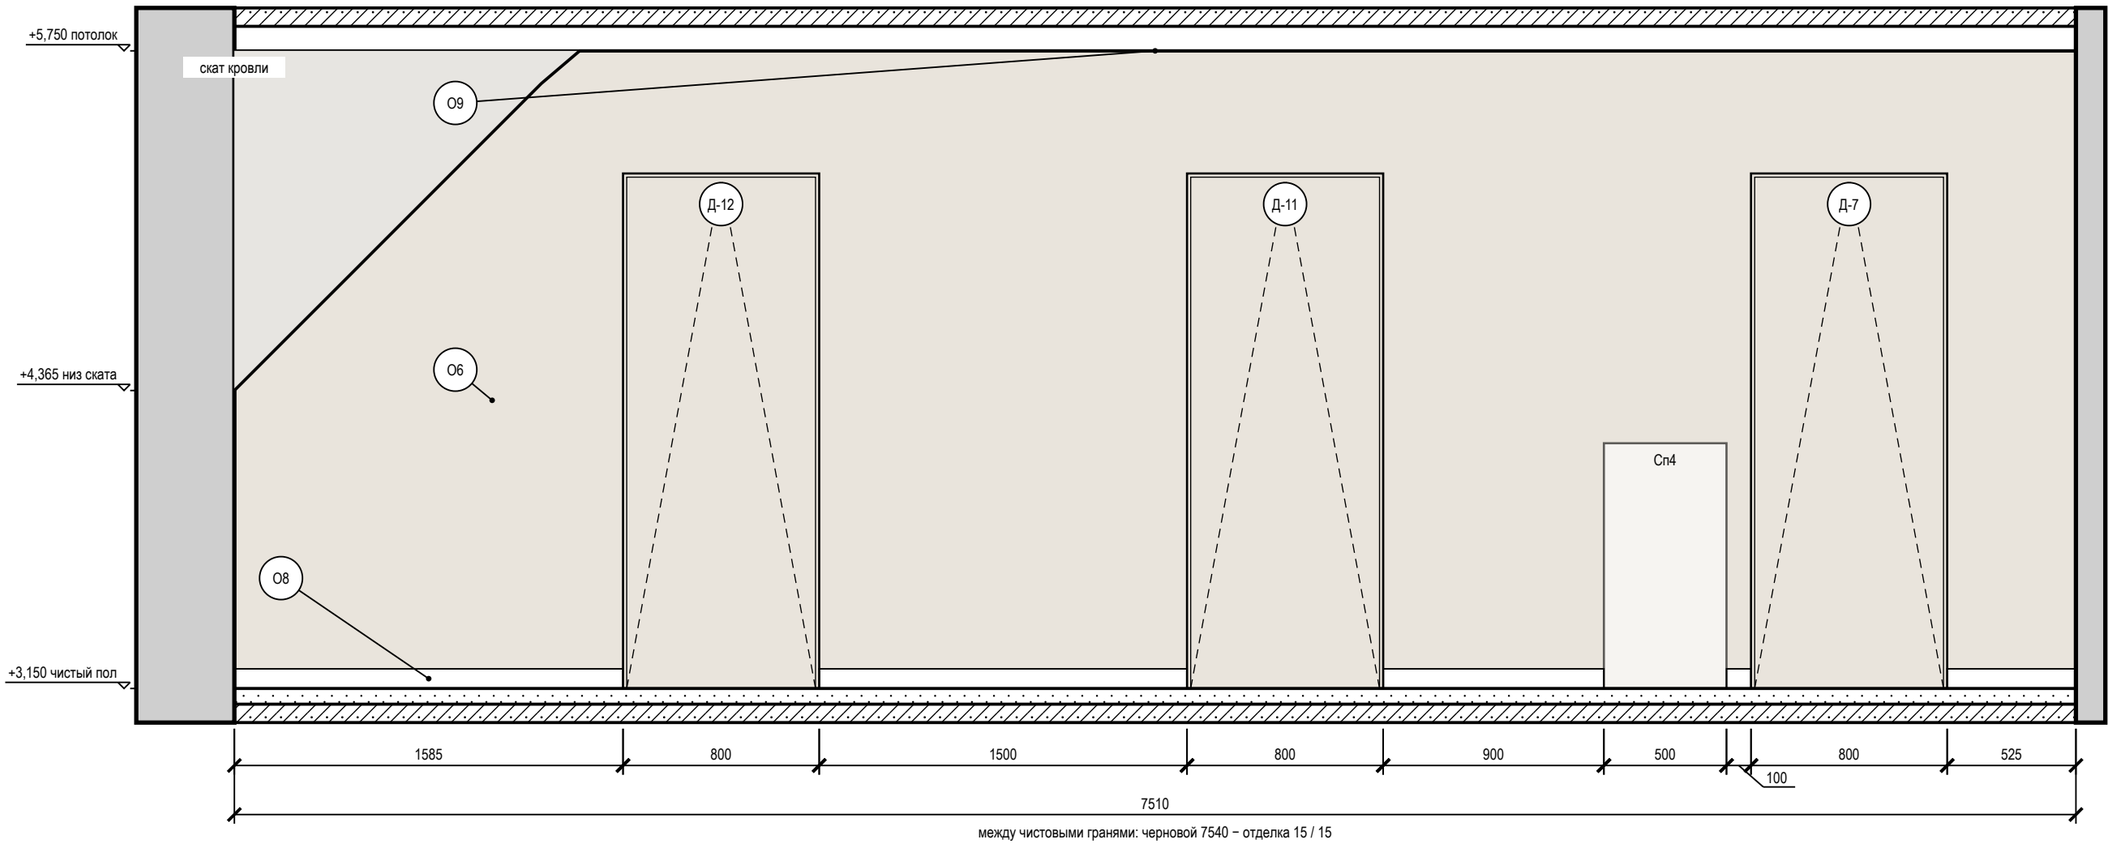

между чистовыми гранями: черновой 7540 − отделка 15 / 15

Условные обозначения

обозначения этого вида, схема развёрток помещения и ведомость отделки — на листе 189

Допущения и предложения на листе

Основа листа: размеры и контуры этажей подобраны проектировщиком по составу помещений и площадям этажей с картинки 470 px (размеры на ней не читаются); обмер и исходный проект — задание (К-1); высоты: 1-й этаж 2800 мм, мансарда 2700 мм (горизонтальная часть) приняты; скаты кровли мансарды приняты по картинке: колено 1200 мм, уклон 45°, конёк вдоль длинной стороны; проект КР — задание (К-2); наружные стены 400 мм, перегородки 120 мм приняты (К-1); разрешённая мощность 15 кВт принята по типовым ТУ для частного дома (К-4); подрайон климата не задан — принят не северный (жилые от 2,5 м) (К-7).

Знак «*» — принято, не замерено и не подтверждено (замерить на объекте): К-2: отметка чистого пола этажа «Мансарда» +3,150 — принята без источника, все отметки мансарды считаются от неё. См. лист открытых вопросов (лист 8, записи К-1, К-2, К-4, К-7).

Примечания

1. Развёртки — вид на стену изнутри помещения, по часовой стрелке; расположение — на схеме листа 189 и на листе 128; размеры — в мм по чистовым поверхностям; отметки — в м от ±0,000 (чистый пол 1-го этажа); высоты Н — от чистого пола помещения до оси изделия, у декора — до центра.
2. Схема мебели, приборов и декора не является технической документацией для производства мебели; габариты — по паспортам изделий.
3. Двери скрытого монтажа — полотно в плоскости стены, отделка стены по полотну, плинтус прерывается у короба (узел — на листе узлов).

1000 мм · печать 1:1

Изм.	Кол.уч	Лист	№ док.	Подп.	Дата
Разраб.		Кырлан А.С.			04.11.26
Пров.					
ГИП					
Н. контр.					
Утв.					

ГД-2026-010-АИ

Дом 331 м²

Общая площадь 270,67* м² · * размеры приняты, не замерены (реестр — л. 8–10, К-1)

Дизайн-проект интерьера

Стадия	Лист	Листов
РП	188	216

Развёртка стены Г. Холл мансарды (пом. 17)

М 1:25


Кырлан Александр Сергеевич

выпуск 04.11.2026 № 2a77323a49 · стр. 192 из 221

Развёртка стены Г: схема и ведомость отделки. Холл мансарды (пом. 17)

ПРЕДВАРИТЕЛЬНО · не для производства работ · открыто пунктов: 15 (реестр — л. 8–10)

Схема развёрток (М 1:50)

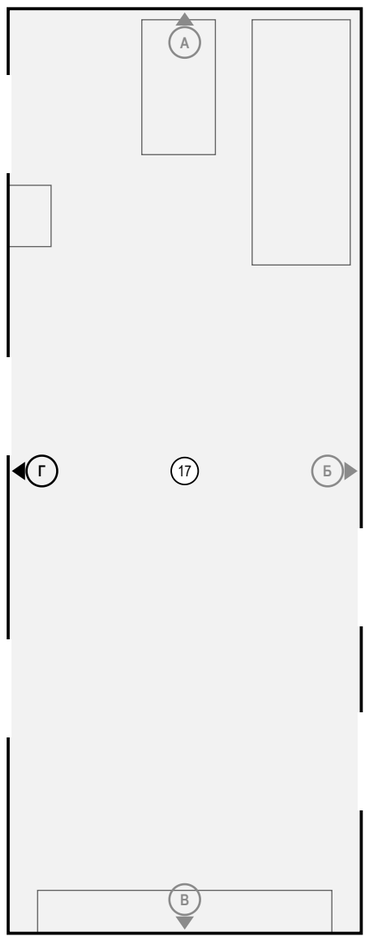

Условные обозначения

- мебель и приборы — фасад по расстановке (условно)
- дверь скрытого монтажа: полотно в плоскости стены (узел — на листе узлов)
- стены и перекрытия в сечении
- окраска: тон — цвет по коду производителя (условно)
- О1 — марка отделки по реестру отделки альбома
- А — марка развёртки: буква стены, стрелка — взгляд

Ведомость отделки (на листе)

Марка	Поверхность	Материал, изделие	Цвет, код	Кол.
О6	стены	окраска, Farrow & Ball Modern Emulsion, матовая, подготовка Q3	Farrow & Ball No. 226 «Joa's White»	14,5 м²
О8	плинтус	плинтус МДФ, h 80 мм, аналог: плинтус МДФ под покраску 80×16	Farrow & Ball No. 226 «Joa's White»	4,6 м
О9	потолок	окраска, Little Greene Absolute Matt, глубокоматовая, подготовка Q3	Little Greene No. 105 «Slaked Lime»	21,7 м²

Примечания

1. Схема, условные обозначения и ведомость отделки — к развёртке стены Г на листе 188: вид в своём масштабе занимает лист целиком.
2. Расположение развёрток всех помещений — на листе 128; полная ведомость отделки — на листах отделочника.

Допущения и предложения на листе

Основа листа: размеры и контуры этажей подобраны проектировщиком по составу помещений и площадям этажей с картинки 470 px (размеры на ней не читаются); обмер и исходный проект — задание (К-1); высоты: 1-й этаж 2800 мм, мансарда 2700 мм (горизонтальная часть) приняты; скаты кровли мансарды приняты по картинке: колено 1200 мм, уклон 45°, конёк вдоль длинной стороны; проект КР — задание (К-2); наружные стены 400 мм, перегородки 120 мм приняты (К-1); разрешённая мощность 15 кВт принята по типовым ТУ для частного дома (К-4); подрайон климата не задан — принят не северный (жилые от 2,5 м) (К-7).

Знак «*» — принято, не замерено и не подтверждено (замерить на объекте): К-2: отметка чистого пола этажа «Мансарда» +3,150 — принята без источника, все отметки мансарды считаются от неё.

Знак «**» — предложение проектировщика, заказчиком не утверждено (согласовать с заказчиком): плинтус пом. 17 — артикул изделия не выбран: позиция описана характеристиками («аналог по характеристикам»), артикул выбирается при закупке.

См. лист открытых вопросов (лист 8, записи К-1, К-2, К-4, К-7).

Изм.	Кол.уч	Лист	№ док.	Подп.	Дата
Разраб.		Кырлан А.С.			04.11.26
Пров.					
ГИП					
Н. контр.					
Утв.					

ГД-2026-010-АИ

Дом 331 м²

Общая площадь 270,67* м² · * размеры приняты, не замерены (реестр — л. 8–10, К-1)

Дизайн-проект интерьера

Стадия	Лист	Листов
РП	189	216

Развёртка стены Г: схема и ведомость отделки. Холл мансарды (пом. 17)

М б/м

Кырлан Александр Сергеевич


выпуск 04.11.2026 № 2a77323a49 · стр. 193 из 221

Развёртка стены А. Спальня 3 (пом. 18)

Спальня 3 (пом. 18) · вид изнутри помещения · размеры в мм, отметки в м от ±0,000 (чистый пол 1-го этажа)

ПРЕДВАРИТЕЛЬНО · не для производства работ · открыто пунктов: 15 (реестр — л. 8–10)

Развёртка стены А

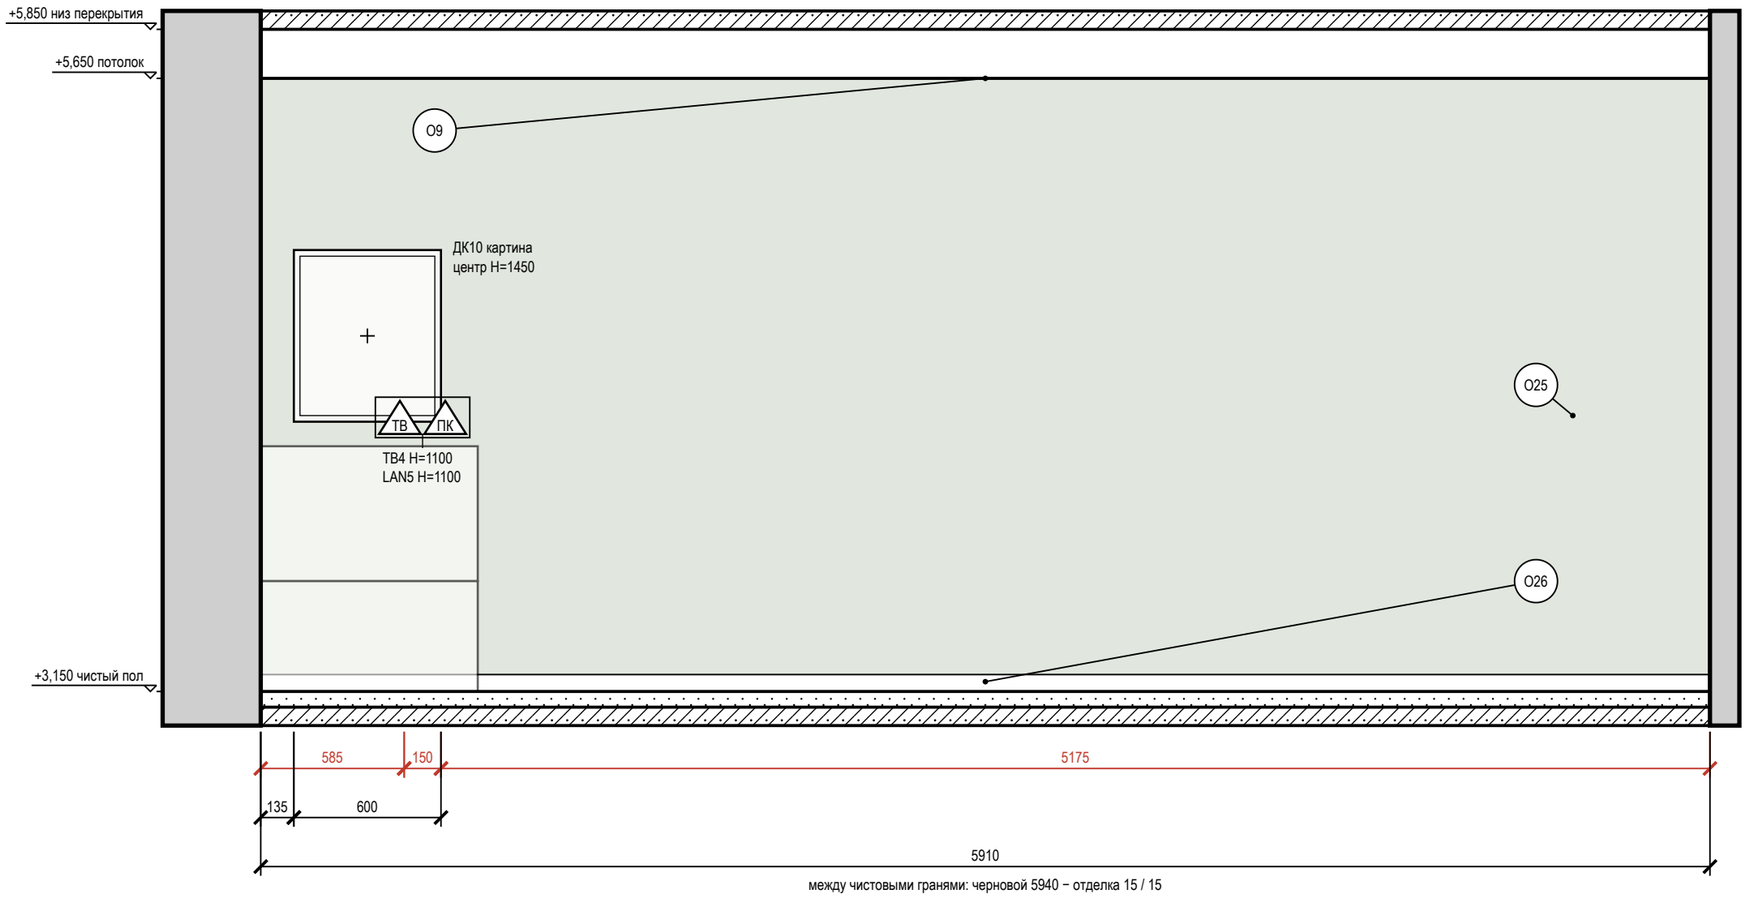


между чистовыми гранями: черновой 5940 − отделка 15 / 15

Условные обозначения

- ПК — розетка компьютерная RJ45
- ТВ — розетка телевизионная
- привязки точек и выводов от угла и от пола, мм
- мебель и приборы — фасад по расстановке (условно)
- картина (декор): марка Д, крест — центр, Н — высота центра, мм
- стены и перекрытия в сечении
- окраска: тон — цвет по коду производителя (условно)
- О1 — марка отделки по реестру отделки альбома
- А — марка развёртки: буква стены, стрелка — взгляд

Схема развёрток (М 1:100)

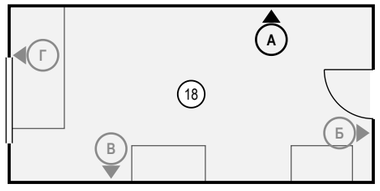

Ведомость отделки (на листе)

Марка	Поверхность	Материал, изделие	Цвет, код	Кол.
О9	потолок	окраска, Little Greene Absolute Matt, глубокоматовая, подготовка Q3	Little Greene No. 105 «Slaked Lime»	17,1 м²
О25	акцентная стена	окраска, Tikkurila Optiva 5 Matt, матовая, подготовка Q3	NCS S 3020-G30Y «S 3020-G30Y»	14,8 м²
О26	плинтус	плинтус МДФ, Orac Decor Contour (Luxxus), h 69 мм, SX165	Farrow & Ball No. 226 «Joa's White»	5,9 м

Допущения и предложения на листе

Основа листа: размеры и контуры этажей подобраны проектировщиком по составу помещений и площадям этажей с картинки 470 px (размеры на ней не читаются); обмер и исходный проект — задание (К-1); высоты: 1-й этаж 2800 мм, мансарда 2700 мм (горизонтальная часть) приняты; скаты кровли мансарды приняты по картинке: колено 1200 мм, уклон 45°, конёк вдоль длинной стороны; проект КР — задание (К-2); наружные стены 400 мм, перегородки 120 мм приняты (К-1); разрешённая мощность 15 кВт принята по типовым ТУ для частного дома (К-4); подрайон климата не задан — принят не северный (жилые от 2,5 м) (К-7).
Знак «*» — принято, не замерено и не подтверждено (замерить на объекте): К-2: отметка чистого пола этажа «Мансарда» +3,150 — принята без источника, все отметки мансарды считаются от неё.
См. лист открытых вопросов (лист 8, записи К-1, К-2, К-4, К-7).

Примечания

1. Развёртки — вид на стену изнутри помещения, по часовой стрелке; расположение — на схеме листа и на листе 128; размеры — в мм по чистовым поверхностям; отметки — в м от ±0,000 (чистый пол 1-го этажа); высоты Н — от чистого пола помещения до оси изделия, у декора — до центра.
2. Красная цепочка — привязки электроточек и выводов по осям от угла чистовых стен; высота Н — у знака, от чистого пола до оси; высоты мебели, проёмов и границ отделки — колонкой отметок слева. Стена с 5 и более точками или с мелкими звеньями привязок показана двумя видами: архитектурная развёртка (мебель, отделка, проёмы, высоты) и вид «Привязки» на отдельном листе — точки и выводы с марками, одна цепочка по осям и таблица привязок (каждая точка — строка).
3. У знака электроточки: марка (Р — розетка, S — выключатель, Св — светильник, ЭВ — вывод кабеля), ×N — число постов в рамке, гр. — группа щита, Н — высота оси от чистого пола, мм; группы по клавишам выключателя — на листе выключателей.
4. Схема мебели, приборов и декора не является технической документацией для производства мебели; габариты — по паспортам изделий.
5. Картины и зеркала крепить к основанию по паспорту изделия (закладные и анкеры — в перечне скрытых работ); крест — ось центра предмета.
6. Потолок — у каждой стены свой, по плану потолков (ПТ5); ступени — зоной, кромка короба перед нишей — тонкой линией; в поле потолка: ПТ6 +5,750.

1000 мм · печать 1:1

Изм.	Кол.уч	Лист	№ док.	Подп.	Дата
Разраб.		Кырлан А.С.			04.11.26
Пров.					
ГИП					
Н. контр.					
Утв.					

ГД-2026-010-АИ

Дом 331 м²

Общая площадь 270,67* м² · * размеры приняты, не замерены (реестр — л. 8–10, К-1)

Дизайн-проект интерьера	Стадия	Лист	Листов
	РП	190	216

Развёртка стены А. Спальня 3 (пом. 18)

М 1:25

Кырлан Александр Сергеевич


выпуск 04.11.2026 № 2a77323a49 · стр. 194 из 221

Развёртка стены Б. Спальня 3 (пом. 18)

Спальня 3 (пом. 18) · вид изнутри помещения · размеры в мм, отметки в м от ±0,000 (чистый пол 1-го этажа)


ПРЕДВАРИТЕЛЬНО · не для производства работ · открыто пунктов: 15 (реестр — л. 8–10)

Развёртка стены Б

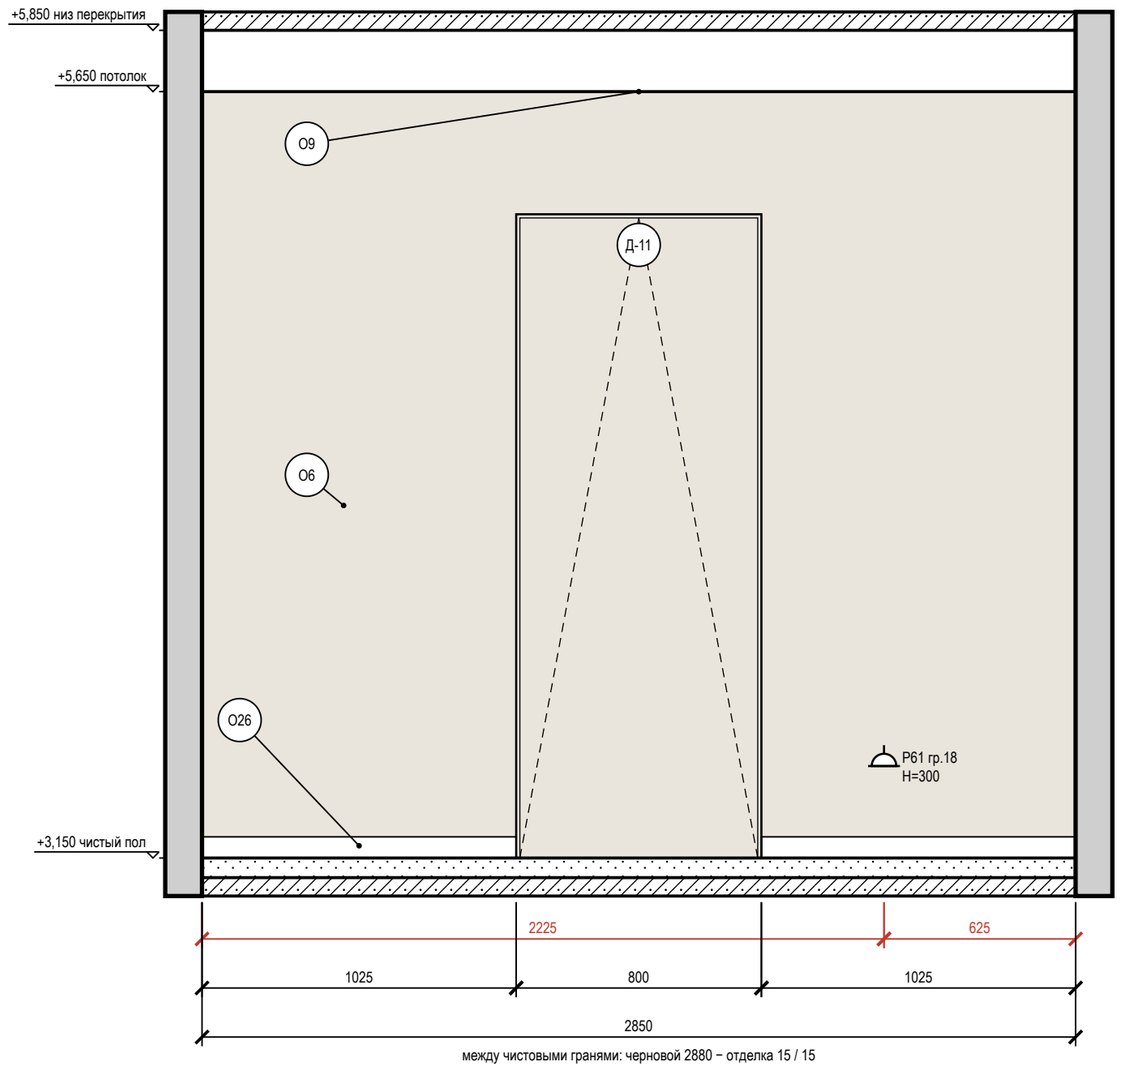

между чистовыми гранями: черновой 2880 − отделка 15 / 15

Схема развёрток (М 1:100)

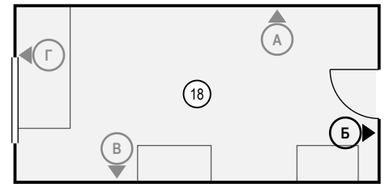

Условные обозначения

- розетка с заземляющим контактом; у знака — марка, ×N постов в рамке, гр. — группа щита, H — высота оси, мм
- привязки точек и выводов от угла и от пола, мм
- мебель и приборы — фасад по расстановке (условно)
- дверь скрытого монтажа: полотно в плоскости стены (узел — на листе узлов)
- стены и перекрытия в сечении
- окраска: тон — цвет по коду производителя (условно)
- О1 — марка отделки по реестру отделки альбома
- А — марка развёртки: буква стены, стрелка — взгляд

Ведомость отделки (на листе)

Марка	Поверхность	Материал, изделие	Цвет, код	Кол.
О6	стены	окраска, Farrow & Ball Modern Emulsion, матовая, подготовка Q3	Farrow & Ball No. 226 «Joa's White»	5,4 м²
О9	потолок	окраска, Little Greene Absolute Matt, глубокоматовая, подготовка Q3	Little Greene No. 105 «Slaked Lime»	17,1 м²
О26	плинтус	плинтус МДФ, Orac Decor Contour (Luxxus), h 69 мм, SX165	Farrow & Ball No. 226 «Joa's White»	2 м

Допущения и предложения на листе

Основа листа: размеры и контуры этажей подобраны проектировщиком по составу помещений и площадям этажей с картинки 470 px (размеры на ней не читаются); обмер и исходный проект — задание (К-1); высоты: 1-й этаж 2800 мм, мансарда 2700 мм (горизонтальная часть) приняты; скаты кровли мансарды приняты по картинке: колено 1200 мм, уклон 45°, конёк вдоль длинной стороны; проект КР — задание (К-2); наружные стены 400 мм, перегородки 120 мм приняты (К-1); разрешённая мощность 15 кВт принята по типовым ТУ для частного дома (К-4); подрайон климата не задан — принят не северный (жилые от 2,5 м) (К-7).

Знак «*» — принято, не замерено и не подтверждено (замерить на объекте): К-2: отметка чистого пола этажа «Мансарда» +3,150 — принята без источника, все отметки мансарды считаются от неё. См. лист открытых вопросов (лист 8, записи К-1, К-2, К-4, К-7).

Примечания

1. Развёртки — вид на стену изнутри помещения, по часовой стрелке; расположение — на схеме листа и на листе 128; размеры — в мм по чистовым поверхностям; отметки — в м от ±0,000 (чистый пол 1-го этажа); высоты H — от чистого пола помещения до оси изделия, у декора — до центра.
2. Красная цепочка — привязки электроточек и выводов по осям от угла чистовых стен; высота H — у знака, от чистого пола до оси; высоты мебели, проёмов и границ отделки — колонкой отметок слева. Стена с 5 и более точками или с мелкими звеньями привязок показана двумя видами: архитектурная развёртка (мебель, отделка, проёмы, высоты) и вид «Привязки» на отдельном листе — точки и выводы с марками, одна цепочка по осям и таблица привязок (каждая точка — строка).
3. У знака электроточки: марка (Р — розетка, S — выключатель, Св — светильник, ЭВ — вывод кабеля), ×N — число постов в рамке, гр. — группа щита, H — высота оси от чистого пола, мм; группы по клавишам выключателя — на листе выключателей.
4. Схема мебели, приборов и декора не является технической документацией для производства мебели; габариты — по паспортам изделий.
5. Двери скрытого монтажа — полотно в плоскости стены, отделка стены по полотну, плинтус прерывается у короба (узел — на листе узлов).
6. Потолок — у каждой стены свой, по плану потолков (ПТ5); ступени — зоной, кромка короба перед нишей — тонкой линией; в поле потолка: ПТ6 +5,750.

1000 мм · печать 1:1

Изм.	Кол.уч	Лист	№ док.	Подп.	Дата
Разраб.		Кырлан А.С.			04.11.26
Пров.					
ГИП					
Н. контр.					
Утв.					

ГД-2026-010-АИ

Дом 331 м²

Общая площадь 270,67* м² · * размеры приняты, не замерены (реестр — л. 8–10, К-1)

Дизайн-проект интерьера

Стадия	Лист	Листов
РП	191	216

Развёртка стены Б. Спальня 3 (пом. 18)

М 1:20

Кырлан Александр Сергеевич


выпуск 04.11.2026 № 2a77323a49 · стр. 195 из 221

Развёртка стены В. Спальня 3 (пом. 18)

Спальня 3 (пом. 18) · вид изнутри помещения · размеры в мм, отметки в м от ±0,000 (чистый пол 1-го этажа)

ПРЕДВАРИТЕЛЬНО · не для производства работ · открыто пунктов: 15 (реестр — л. 8–10)

Развёртка стены В

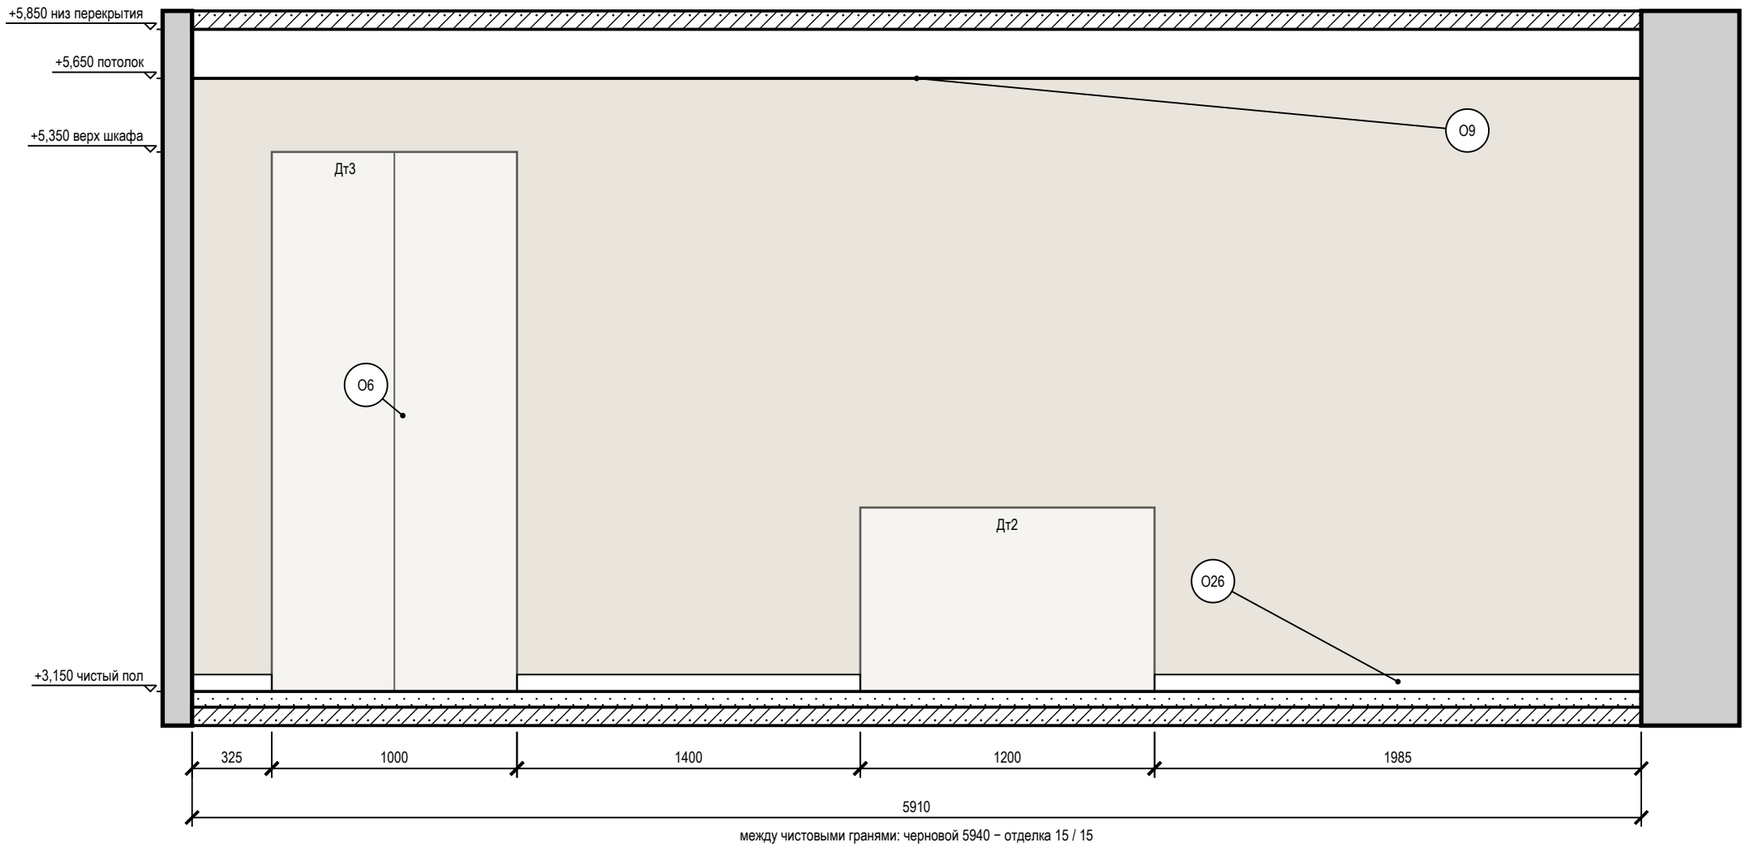


между чистовыми гранями: черновой 5940 − отделка 15 / 15

Условные обозначения

- мебель и приборы — фасад по расстановке (условно)
- стены и перекрытия в сечении
- окраска: тон — цвет по коду производителя (условно)
- О1 — марка отделки по реестру отделки альбома
- А — марка развёртки: буква стены, стрелка — взгляд

Схема развёрток (М 1:100)

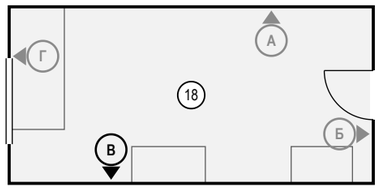

Ведомость отделки (на листе)

Марка	Поверхность	Материал, изделие	Цвет, код	Кол.
О6	стены	окраска, Farrow & Ball Modern Emulsion, матовая, подготовка Q3	Farrow & Ball No. 226 «Joa's White»	14,8 м²
О9	потолок	окраска, Little Greene Absolute Matt, глубокоматовая, подготовка Q3	Little Greene No. 105 «Slaked Lime»	17,1 м²
О26	плинтус	плинтус МДФ, Orac Decor Contour (Luxxus), h 69 мм, SX165	Farrow & Ball No. 226 «Joa's White»	3,7 м

Допущения и предложения на листе

Основа листа: размеры и контуры этажей подобраны проектировщиком по составу помещений и площадям этажей с картинки 470 px (размеры на ней не читаются); обмер и исходный проект — задание (К-1); высоты: 1-й этаж 2800 мм, мансарда 2700 мм (горизонтальная часть) приняты; скаты кровли мансарды приняты по картинке: колено 1200 мм, уклон 45°, конёк вдоль длинной стороны; проект КР — задание (К-2); наружные стены 400 мм, перегородки 120 мм приняты (К-1); разрешённая мощность 15 кВт принята по типовым ТУ для частного дома (К-4); подрайон климата не задан — принят не северный (жилые от 2,5 м) (К-7).
Знак «*» — принято, не замерено и не подтверждено (замерить на объекте): К-2: отметка чистого пола этажа «Мансарда» +3,150 — принята без источника, все отметки мансарды считаются от неё.
См. лист открытых вопросов (лист 8, записи К-1, К-2, К-4, К-7).

Примечания

1. Развёртки — вид на стену изнутри помещения, по часовой стрелке; расположение — на схеме листа и на листе 128; размеры — в мм по чистовым поверхностям; отметки — в м от ±0,000 (чистый пол 1-го этажа); высоты Н — от чистого пола помещения до оси изделия, у декора — до центра.
2. Стена В показана двумя видами: здесь — архитектурная развёртка (мебель, отделка, проёмы, высоты), электроточки и выводы ВК с привязками и таблицей — на листе 193 («Привязки»).
3. Схема мебели, приборов и декора не является технической документацией для производства мебели; габариты — по паспортам изделий.
4. Потолок — у каждой стены свой, по плану потолков (ПТ5); ступени — зоной, кромка короба перед нишей — тонкой линией; в поле потолка: ПТ6 +5,750.

1000 мм · печать 1:1

Изм.	Кол.уч	Лист	№ док.	Подп.	Дата
Разраб.		Кырлан А.С.			04.11.26
Пров.					
ГИП					
Н. контр.					
Утв.					

ГД-2026-010-АИ

Дом 331 м²

Общая площадь 270,67* м² · * размеры приняты, не замерены (реестр — л. 8–10, К-1)

Дизайн-проект интерьера

Стадия	Лист	Листов
РП	192	216

Развёртка стены В. Спальня 3 (пом. 18)

М 1:25

Кырлан Александр Сергеевич

выпуск 04.11.2026 № 2a77323a49 · стр. 196 из 221

Привязки электроточек, стена В. Спальня 3 (пом. 18)

Спальня 3 (пом. 18) · вид изнутри помещения · привязки в мм, отметки в м · к развёртке на листе 192

ПРЕДВАРИТЕЛЬНО · не для производства работ · открыто пунктов: 15 (реестр — л. 8–10)

Развёртка стены В: электроточки и выводы

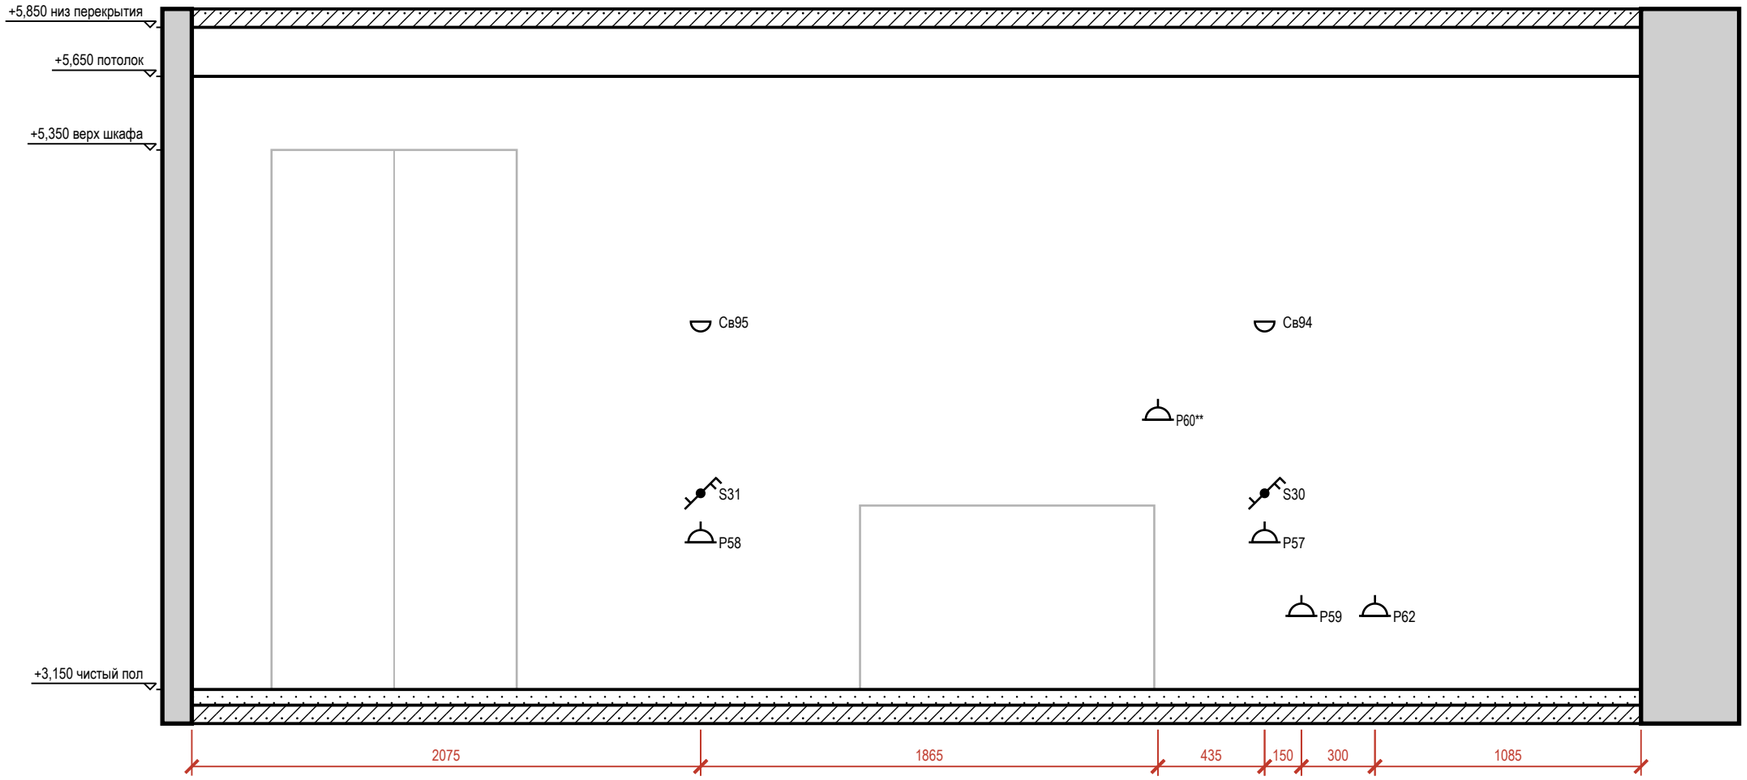


Таблица привязок электроточек и выводов

Марка	Назначение	От угла, мм	Н от пола, мм	Примечание
P58	розетка: у кровати	2075	600	гр. 18
S31	выключатель	2075	800	гр. 1
Св95	светильник настенный	2075	1500	гр. 1
P60**	розетка: ТВ над комодом (в одной зоне с ТВ4, LAN5)	3940	1100	гр. 18
P57	розетка: у кровати	4375	600	гр. 18

Марка	Назначение	От угла, мм	Н от пола, мм	Примечание
S30	выключатель	4375	800	гр. 1
Св94	светильник настенный	4375	1500	гр. 1
P59	розетка: у комода	4525	300	гр. 18
P62	розетка: уборка у входа	4825	300	гр. 18

Условные обозначения

- розетка с заземляющим контактом; у знака — марка, ×N постов в рамке, гр. — группа щита, Н — высота оси, мм
- выключатель одноклавишный
- выключатель двухклавишный (флажков — по числу клавиш)
- выключатель с проходной или перекрёстной клавишей (обратный флажок); тип клавиши — в подписи
- светильник настенный (бра), Н — высота оси
- привязки точек и выводов от угла и от пола, мм

Примечания

1. Вид «Привязки» стены В — электроточки и выводы ВК; архитектурная развёртка (мебель, отделка, проёмы, высоты) — на листе 192, расположение — на листе 128. Мебель и приборы — подложкой для ориентира; их марки и обозначения мебели, проёмов и стен — там же.
2. Привязки — в мм: по горизонтали от левого чистового угла стены до оси изделия, Н — от чистого пола до оси; все точки — в таблице привязок. Красная цепочка — привязки по осям; точки ближе 150 мм одна к другой в цепочку не дробятся — их привязки только в таблице.
3. У знака — марка электроточки (Р — розетка, S — выключатель, Св — светильник, ЭВ — вывод кабеля); посты в рамке и группа щита — в графе «Примечание»; группы по клавишам выключателя — на листе выключателей.

Допущения и предложения на листе

Основа листа: размеры и контуры этажей подобраны проектировщиком по составу помещений и площадям этажей с картинки 470 px (размеры на ней не читаются); обмер и исходный проект — задание (К-1); высоты: 1-й этаж 2800 мм, мансарда 2700 мм (горизонтальная часть) приняты; скаты кровли мансарды приняты по картинке: колено 1200 мм, уклон 45°, конёк вдоль длинной стороны; проект КР — задание (К-2); наружные стены 400 мм, перегородки 120 мм приняты (К-1); разрешённая мощность 15 кВт принята по типовым ТУ для частного дома (К-4); подрайон климата не задан — принят не северный (жилые от 2,5 м) (К-7).

Знак «*» — принято, не замерено и не подтверждено (замерить на объекте): К-2: отметка чистого пола этажа «Мансарда» +3,150 — принята без источника, все отметки мансарды считаются от неё.

Знак «**» — предложение проектировщика, заказчиком не утверждено (согласовать с заказчиком): Р60 — высота 1100 мм выше нормы 1 м (ПУЭ 6.6.30) по назначению: питание ТВ над комодом, в одной зоне с выводами ТВ4 и LAN5.

См. лист открытых вопросов (лист 8, записи К-1, К-2, К-4, К-7).

1000 мм · печать 1:1

Изм.	Кол.уч	Лист	№ док.	Подп.	Дата
Разраб.		Кырлан А.С.			04.11.26
Пров.					
ГИП					
Н. контр.					
Утв.					

ГД-2026-010-АИ

Дом 331 м²

Общая площадь 270,67* м² · * размеры приняты, не замерены (реестр — л. 8–10, К-1)

Дизайн-проект интерьера

Стадия	Лист	Листов
РП	193	216

Привязки электроточек, стена В. Спальня 3 (пом. 18)

М 1:25

Кырлан Александр Сергеевич

выпуск 04.11.2026 № 2a77323a49 · стр. 197 из 221

Развёртка стены Г. Спальня 3 (пом. 18)

Спальня 3 (пом. 18) · вид изнутри помещения · размеры в мм, отметки в м от ±0,000 (чистый пол 1-го этажа)

ПРЕДВАРИТЕЛЬНО · не для производства работ · открыто пунктов: 15 (реестр — л. 8–10)

Развёртка стены Г


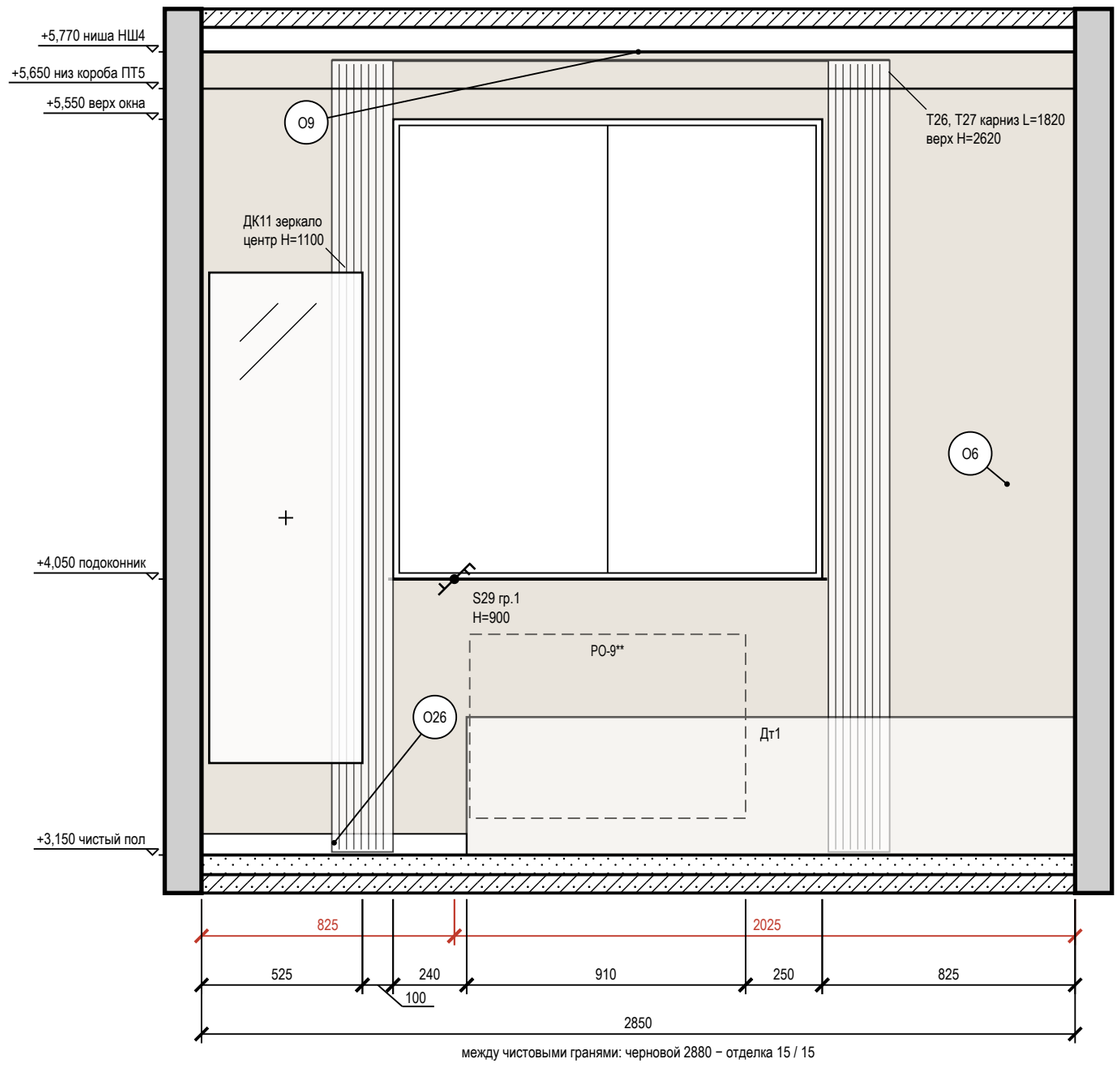


Схема развёрток (М 1:100)

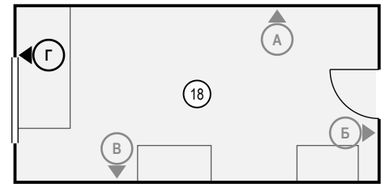

Условные обозначения

- выключатель одноклавишный
- выключатель двухклавишный (флажков — по числу клавиш)
- выключатель с проходной или перекрёстной клавишей (обратный флажок); тип клавиши — в подписи
- привязки точек и выводов от угла и от пола, мм
- мебель и приборы — фасад по расстановке (условно)
- зеркало: марка Д, крест — центр, Н — высота центра, мм
- карниз (шина) и шторы в собранном виде: марка Т, длина L, верх Н
- окно: проём, рама, подоконник
- радиатор отопления; марка — по плану отопления
- стены и перекрытия в сечении
- окраска: тон — цвет по коду производителя (условно)
- О1 — марка отделки по реестру отделки альбома
- А — марка развёртки: буква стены, стрелка — взгляд

Ведомость отделки (на листе)

Марка	Поверхность	Материал, изделие	Цвет, код	Кол.
О6	стены	окраска, Farrow & Ball Modern Emulsion, матовая, подготовка Q3	Farrow & Ball No. 226 «Joa's White»	5,4 м²
О9	потолок	окраска, Little Greene Absolute Matt, глубокоматовая, подготовка Q3	Little Greene No. 105 «Slaked Lime»	17,1 м²
О26	плинтус	плинтус МДФ, Orac Decor Contour (Luxxus), h 69 мм, SX165	Farrow & Ball No. 226 «Joa's White»	0,9 м

Допущения и предложения на листе. Основа листа: размеры и контуры этажей подобраны проектировщиком по составу помещений и площадям этажей с картинки 470 px (размеры на ней не читаются); обмер и исходный проект — задание (К-1); высоты: 1-й этаж 2800 мм, мансарда 2700 мм (горизонтальная часть) приняты; скаты кровли мансарды приняты по картинке: колено 1200 мм, уклон 45°, конёк вдоль длинной стороны; проект КР — задание (К-2); наружные стены 400 мм, перегородки 120 мм приняты (К-1); разрешённая мощность 15 кВт принята по типовым ТУ для частного дома (К-4); подрайон климата не задан — принят не северный (жилые от 2,5 м) (К-7). Знак «*» — принято, не замерено и не подтверждено (замерить на объекте): К-2: отметка чистого пола этажа «Мансарда» +3,150 — принята без источника, все отметки мансарды считаются от неё. Знак «**» — предложение проектировщика, заказчиком не утверждено (согласовать с заказчиком): К-11: РО-9 — прибор под окном по оси проёма, ширина ≈ 0,7 ширины окна — предложение ОВ (лист ОВ выводил его сам до, теперь он в данных — один источник для листа, мебели, DXF и IFC); котёл и мощность не выбраны (К-11) — размер по теплотехническому расчёту. См. лист открытых вопросов (лист 8, записи К-1, К-2, К-4, К-7; лист 9, запись К-11).

Примечания

1. Развёртки — вид на стену изнутри помещения, по часовой стрелке; расположение — на схеме листа и на листе 128; размеры — в мм по чистовым поверхностям; отметки — в м от ±0,000 (чистый пол 1-го этажа); высоты Н — от чистого пола помещения до оси изделия, у декора — до центра.
2. Красная цепочка — привязки электроточек и выводов по осям от угла чистовых стен; высота Н — у знака, от чистого пола до оси; высоты мебели, проёмов и границ отделки — колонкой отметок слева. Стена с 5 и более точками или с мелкими звеньями привязок показана двумя видами: архитектурная развёртка (мебель, отделка, проёмы, высоты) и вид «Привязки» на отдельном листе — точки и выводы с марками, одна цепочка по осям и таблица привязок (каждая точка — строка).
3. У знака электроточки: марка (Р — розетка, S — выключатель, Св — светильник, ЭВ — вывод кабеля), ×N — число постов в рамке, гр. — группа щита, Н — высота оси от чистого пола, мм; группы по клавишам выключателя — на листе выключателей.
4. Схема мебели, приборов и декора не является технической документацией для производства мебели; габариты — по паспортам изделий.
5. Картины и зеркала крепить к основанию по паспорту изделия (закладные и анкеры — в перечне скрытых работ); крест — ось центра предмета.
6. Карнизы (шины) — по ведомости текстиля декоратора: длина L и верх Н на развёртке — те же числа, что в ведомости; крепление — до окраски потолка.
7. Потолок — у каждой стены свой, по плану потолков (НШ4, ПТ5); ступени — зоной, кромка короба перед нишей — тонкой линией; в поле потолка: ПТ6 +5,750.

1000 мм · печать 1:1

Изм.	Кол.уч	Лист	№ док.	Подп.	Дата				
Разраб.		Кырлан А.С.			04.11.26	**ГД-2026-010-АИ**			
Пров.						Дом 331 м²			
ГИП						Общая площадь 270,67* м² · * размеры приняты, не замерены (реестр — л. 8–10, К-1)			
						Дизайн-проект интерьера	Стадия	Лист	Листов
Н. контр.							РП	194	216
Утв.						**Развёртка стены Г. Спальня 3 (пом. 18)** М 1:20	**Кырлан Александр Сергеевич**		


выпуск 04.11.2026 № 2a77323a49 · стр. 198 из 221

Развёртка стены А. Спальня 4 (пом. 19)

Спальня 4 (пом. 19) · вид изнутри помещения · размеры в мм, отметки в м от ±0,000 (чистый пол 1-го этажа)

ПРЕДВАРИТЕЛЬНО · не для производства работ · открыто пунктов: 15 (реестр — л. 8–10)

Развёртка стены А

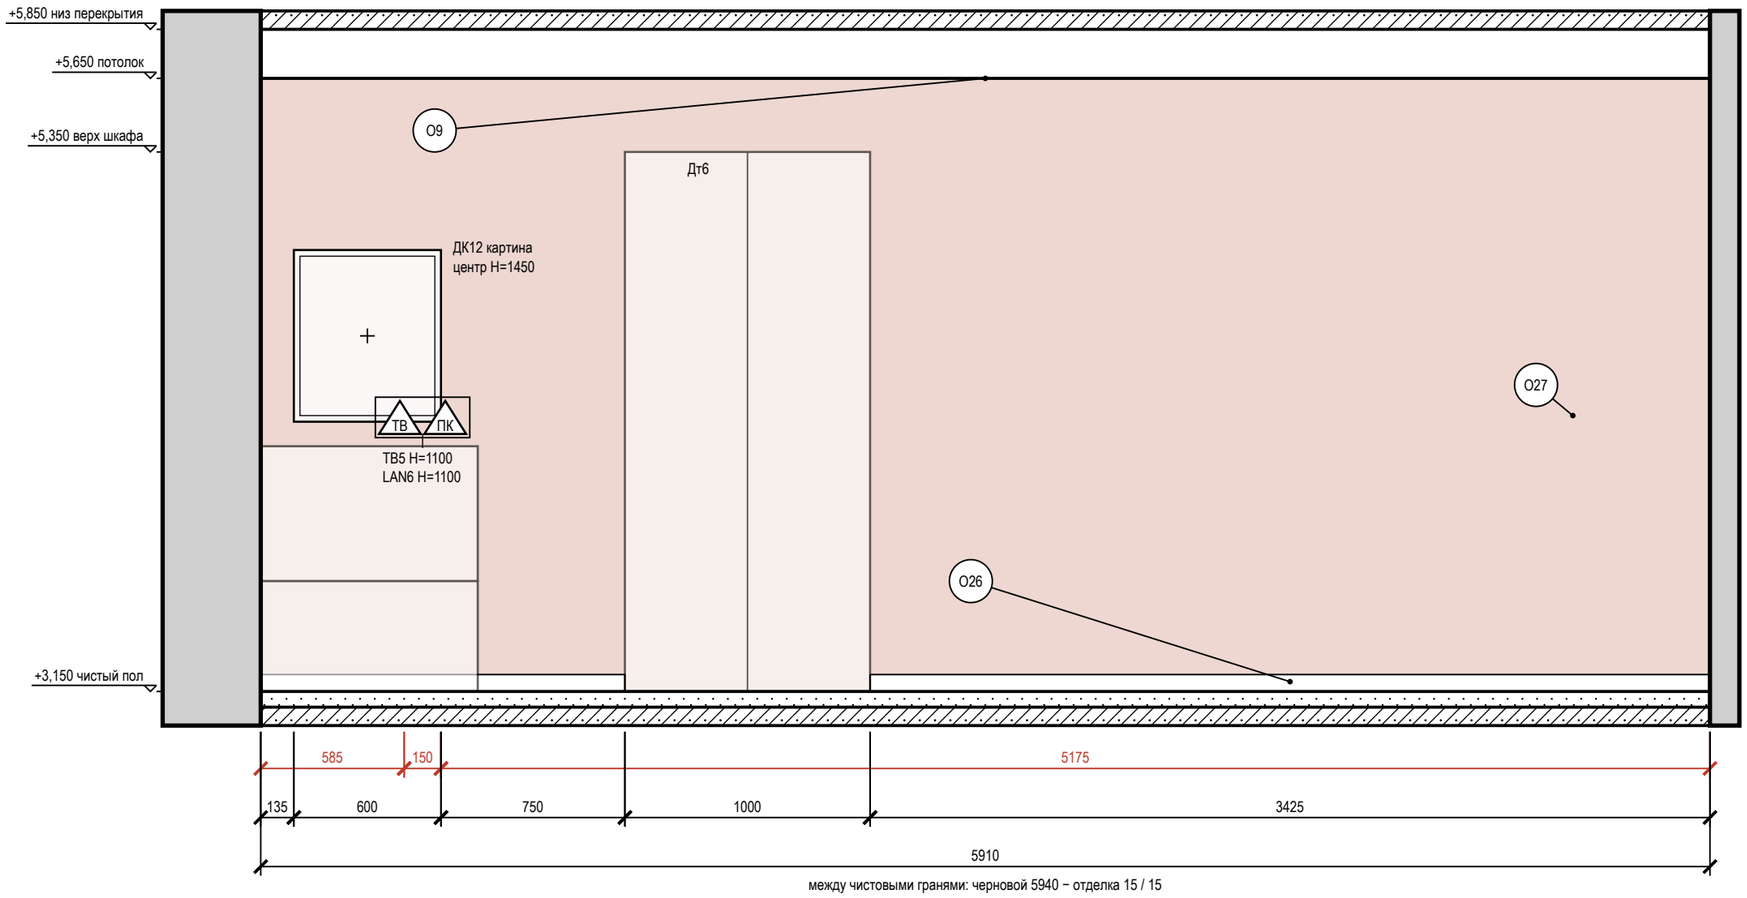


между чистовыми гранями: черновой 5940 − отделка 15 / 15

Условные обозначения

- ПК — розетка компьютерная RJ45
- ТВ — розетка телевизионная
- привязки точек и выводов от угла и от пола, мм
- мебель и приборы — фасад по расстановке (условно)
- картина (декор): марка Д, крест — центр, Н — высота центра, мм
- стены и перекрытия в сечении
- окраска: тон — цвет по коду производителя (условно)
- О1 — марка отделки по реестру отделки альбома
- А — марка развёртки: буква стены, стрелка — взгляд

Схема развёрток (М 1:100)

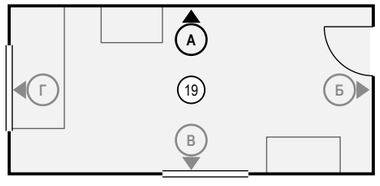

Ведомость отделки (на листе)

Марка	Поверхность	Материал, изделие	Цвет, код	Кол.
О9	потолок	окраска, Little Greene Absolute Matt, глубокоматовая, подготовка Q3	Little Greene No. 105 «Slaked Lime»	16,3 м²
О26	плинтус	плинтус МДФ, Orac Decor Contour (Luxxus), h 69 мм, SX165	Farrow & Ball No. 226 «Joa's White»	4,9 м
О27	акцентная стена	окраска, Tikkurila Optiva 5 Matt, матовая, подготовка Q3	NCS S 3040-Y70R «S 3040-Y70R»	14,8 м²

Допущения и предложения на листе

Основа листа: размеры и контуры этажей подобраны проектировщиком по составу помещений и площадям этажей с картинки 470 px (размеры на ней не читаются); обмер и исходный проект — задание (К-1); высоты: 1-й этаж 2800 мм, мансарда 2700 мм (горизонтальная часть) приняты; скаты кровли мансарды приняты по картинке: колено 1200 мм, уклон 45°, конёк вдоль длинной стороны; проект КР — задание (К-2); наружные стены 400 мм, перегородки 120 мм приняты (К-1); разрешённая мощность 15 кВт принята по типовым ТУ для частного дома (К-4); подрайон климата не задан — принят не северный (жилые от 2,5 м) (К-7).
Знак «*» — принято, не замерено и не подтверждено (замерить на объекте): К-2: отметка чистого пола этажа «Мансарда» +3,150 — принята без источника, все отметки мансарды считаются от неё.
См. лист открытых вопросов (лист 8, записи К-1, К-2, К-4, К-7).

Примечания

1. Развёртки — вид на стену изнутри помещения, по часовой стрелке; расположение — на схеме листа и на листе 128; размеры — в мм по чистовым поверхностям; отметки — в м от ±0,000 (чистый пол 1-го этажа); высоты Н — от чистого пола помещения до оси изделия, у декора — до центра.
2. Красная цепочка — привязки электроточек и выводов по осям от угла чистовых стен; высота Н — у знака, от чистого пола до оси; высоты мебели, проёмов и границ отделки — колонкой отметок слева. Стена с 5 и более точками или с мелкими звеньями привязок показана двумя видами: архитектурная развёртка (мебель, отделка, проёмы, высоты) и вид «Привязки» на отдельном листе — точки и выводы с марками, одна цепочка по осям и таблица привязок (каждая точка — строка).
3. У знака электроточки: марка (Р — розетка, S — выключатель, Св — светильник, ЭВ — вывод кабеля), ×N — число постов в рамке, гр. — группа щита, Н — высота оси от чистого пола, мм; группы по клавишам выключателя — на листе выключателей.
4. Схема мебели, приборов и декора не является технической документацией для производства мебели; габариты — по паспортам изделий.
5. Картины и зеркала крепить к основанию по паспорту изделия (закладные и анкеры — в перечне скрытых работ); крест — ось центра предмета.
6. Потолок — у каждой стены свой, по плану потолков (ПТ5); ступени — зоной, кромка короба перед нишей — тонкой линией; в поле потолка: ПТ6 +5,750.

1000 мм · печать 1:1

Изм.	Кол.уч	Лист	№ док.	Подп.	Дата
Разраб.		Кырлан А.С.			04.11.26
Пров.					
ГИП					
Н. контр.					
Утв.					

ГД-2026-010-АИ

Дом 331 м²

Общая площадь 270,67* м² · * размеры приняты, не замерены (реестр — л. 8–10, К-1)

Дизайн-проект интерьера	Стадия	Лист	Листов
	РП	195	216

Развёртка стены А. Спальня 4 (пом. 19)

М 1:25

Кырлан Александр Сергеевич


выпуск 04.11.2026 № 2a77323a49 · стр. 199 из 221

Развёртка стены Б. Спальня 4 (пом. 19)

Спальня 4 (пом. 19) · вид изнутри помещения · размеры в мм, отметки в м от ±0,000 (чистый пол 1-го этажа)


ПРЕДВАРИТЕЛЬНО · не для производства работ · открыто пунктов: 15 (реестр — л. 8–10)

Развёртка стены Б

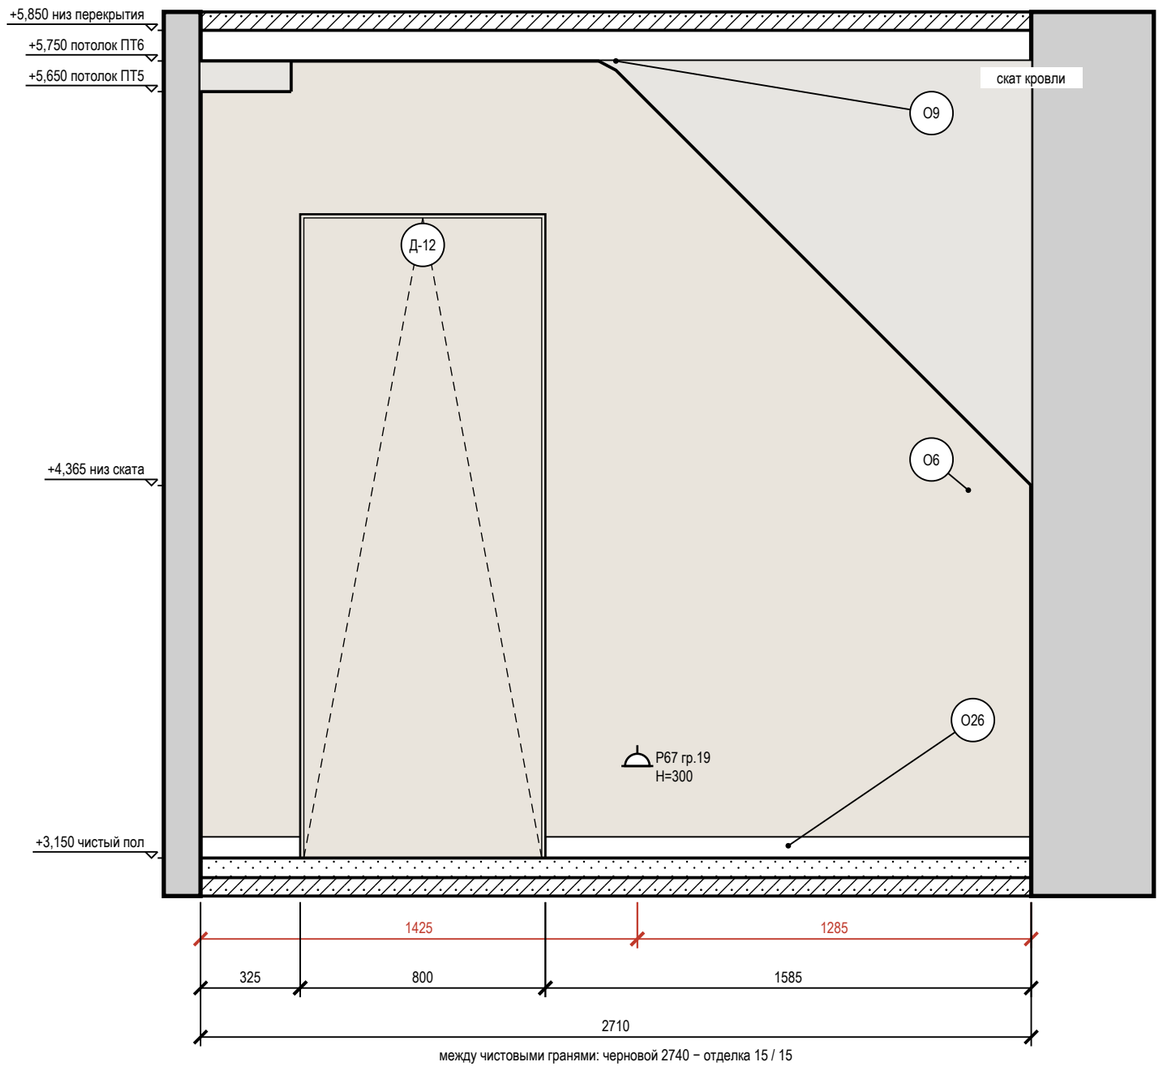

между чистовыми гранями: черновой 2740 − отделка 15 / 15

Схема развёрток (М 1:100)

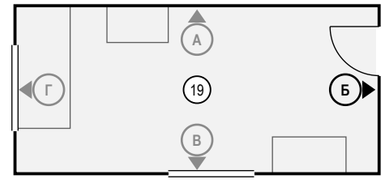

Условные обозначения

- розетка с заземляющим контактом; у знака — марка, ×N постов в рамке, гр. — группа щита, H — высота оси, мм
- привязки точек и выводов от угла и от пола, мм
- мебель и приборы — фасад по расстановке (условно)
- дверь скрытого монтажа: полотно в плоскости стены (узел — на листе узлов)
- стены и перекрытия в сечении
- окраска: тон — цвет по коду производителя (условно)
- О1 — марка отделки по реестру отделки альбома
- А — марка развёртки: буква стены, стрелка — взгляд

Ведомость отделки (на листе)

Марка	Поверхность	Материал, изделие	Цвет, код	Кол.
О6	стены	окраска, Farrow & Ball Modern Emulsion, матовая, подготовка Q3	Farrow & Ball No. 226 «Joa's White»	5,4 м²
О9	потолок	окраска, Little Greene Absolute Matt, глубокоматовая, подготовка Q3	Little Greene No. 105 «Slaked Lime»	16,3 м²
О26	плинтус	плинтус МДФ, Orac Decor Contour (Luxxus), h 69 мм, SX165	Farrow & Ball No. 226 «Joa's White»	1,9 м

Допущения и предложения на листе

Основа листа: размеры и контуры этажей подобраны проектировщиком по составу помещений и площадям этажей с картинки 470 px (размеры на ней не читаются); обмер и исходный проект — задание (К-1); высоты: 1-й этаж 2800 мм, мансарда 2700 мм (горизонтальная часть) приняты; скаты кровли мансарды приняты по картинке: колено 1200 мм, уклон 45°, конёк вдоль длинной стороны; проект КР — задание (К-2); наружные стены 400 мм, перегородки 120 мм приняты (К-1); разрешённая мощность 15 кВт принята по типовым ТУ для частного дома (К-4); подрайон климата не задан — принят не северный (жилые от 2,5 м) (К-7).

Знак «*» — принято, не замерено и не подтверждено (замерить на объекте): К-2: отметка чистого пола этажа «Мансарда» +3,150 — принята без источника, все отметки мансарды считаются от неё. См. лист открытых вопросов (лист 8, записи К-1, К-2, К-4, К-7).

Примечания

1. Развёртки — вид на стену изнутри помещения, по часовой стрелке; расположение — на схеме листа и на листе 128; размеры — в мм по чистовым поверхностям; отметки — в м от ±0,000 (чистый пол 1-го этажа); высоты H — от чистого пола помещения до оси изделия, у декора — до центра.
2. Красная цепочка — привязки электроточек и выводов по осям от угла чистовых стен; высота H — у знака, от чистого пола до оси; высоты мебели, проёмов и границ отделки — колонкой отметок слева. Стена с 5 и более точками или с мелкими звеньями привязок показана двумя видами: архитектурная развёртка (мебель, отделка, проёмы, высоты) и вид «Привязки» на отдельном листе — точки и выводы с марками, одна цепочка по осям и таблица привязок (каждая точка — строка).
3. У знака электроточки: марка (Р — розетка, S — выключатель, Св — светильник, ЭВ — вывод кабеля), ×N — число постов в рамке, гр. — группа щита, H — высота оси от чистого пола, мм; группы по клавишам выключателя — на листе выключателей.
4. Схема мебели, приборов и декора не является технической документацией для производства мебели; габариты — по паспортам изделий.
5. Двери скрытого монтажа — полотно в плоскости стены, отделка стены по полотну, плинтус прерывается у короба (узел — на листе узлов).
6. Потолок — у каждой стены свой, по плану потолков (ПТ6, ПТ5); ступени — зоной, кромка короба перед нишей — тонкой линией.

1000 мм · печать 1:1

Изм.	Кол.уч	Лист	№ док.	Подп.	Дата
Разраб.		Кырлан А.С.			04.11.26
Пров.					
ГИП					
Н. контр.					
Утв.					

ГД-2026-010-АИ

Дом 331 м²

Общая площадь 270,67* м² · * размеры приняты, не замерены (реестр — л. 8–10, К-1)

Дизайн-проект интерьера

Стадия	Лист	Листов
РП	196	216

Развёртка стены Б. Спальня 4 (пом. 19)

М 1:20

Кырлан Александр Сергеевич


выпуск 04.11.2026 № 2a77323a49 · стр. 200 из 221

Развёртка стены В. Спальня 4 (пом. 19)

Спальня 4 (пом. 19) · вид изнутри помещения · размеры в мм, отметки в м от ±0,000 (чистый пол 1-го этажа)

ПРЕДВАРИТЕЛЬНО · не для производства работ · открыто пунктов: 15 (реестр — л. 8–10)

Развёртка стены В

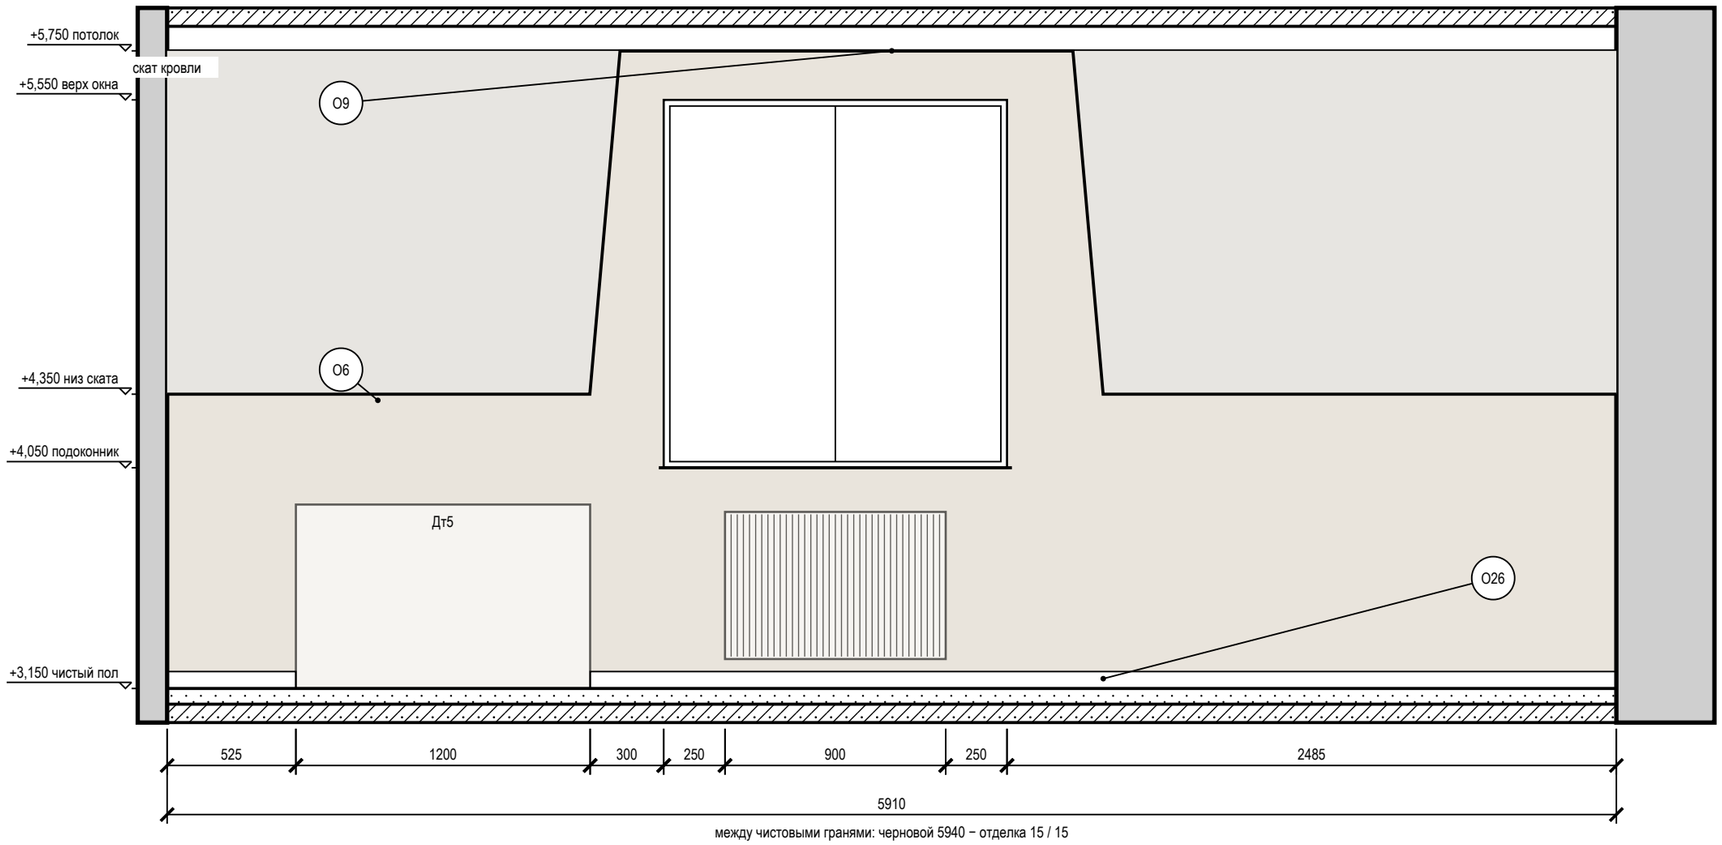


между чистовыми гранями: черновой 5940 − отделка 15 / 15

Условные обозначения

- мебель и приборы — фасад по расстановке (условно)
- окно: проём, рама, подоконник
- радиатор отопления; марка — по плану отопления
- стены и перекрытия в сечении
- окраска: тон — цвет по коду производителя (условно)
- О1 — марка отделки по реестру отделки альбома
- А — марка развёртки: буква стены, стрелка — взгляд

Схема развёрток (М 1:100)

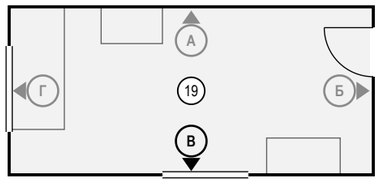

Ведомость отделки (на листе)

Марка	Поверхность	Материал, изделие	Цвет, код	Кол.
О6	стены	окраска, Farrow & Ball Modern Emulsion, матовая, подготовка Q3	Farrow & Ball No. 226 «Joa's White»	13,3 м²
О9	потолок	окраска, Little Greene Absolute Matt, глубокоматовая, подготовка Q3	Little Greene No. 105 «Slaked Lime»	16,3 м²
О26	плинтус	плинтус МДФ, Orac Decor Contour (Luxxus), h 69 мм, SX165	Farrow & Ball No. 226 «Joa's White»	4,7 м

Допущения и предложения на листе

Основа листа: размеры и контуры этажей подобраны проектировщиком по составу помещений и площадям этажей с картинки 470 px (размеры на ней не читаются); обмер и исходный проект — задание (К-1); высоты: 1-й этаж 2800 мм, мансарда 2700 мм (горизонтальная часть) приняты; скаты кровли мансарды приняты по картинке: колено 1200 мм, уклон 45°, конёк вдоль длинной стороны; проект КР — задание (К-2); наружные стены 400 мм, перегородки 120 мм приняты (К-1); разрешённая мощность 15 кВт принята по типовым ТУ для частного дома (К-4); подрайон климата не задан — принят не северный (жилые от 2,5 м) (К-7).
Знак «*» — принято, не замерено и не подтверждено (замерить на объекте): К-2: отметка чистого пола этажа «Мансарда» +3,150 — принята без источника, все отметки мансарды считаются от неё.
См. лист открытых вопросов (лист 8, записи К-1, К-2, К-4, К-7).

Примечания

1. Развёртки — вид на стену изнутри помещения, по часовой стрелке; расположение — на схеме листа и на листе 128; размеры — в мм по чистовым поверхностям; отметки — в м от ±0,000 (чистый пол 1-го этажа); высоты Н — от чистого пола помещения до оси изделия, у декора — до центра.
2. Стена В показана двумя видами: здесь — архитектурная развёртка (мебель, отделка, проёмы, высоты), электроточки и выводы ВК с привязками и таблицей — на листе 198 («Привязки»).
3. Схема мебели, приборов и декора не является технической документацией для производства мебели; габариты — по паспортам изделий.
4. Потолок — у каждой стены свой, по плану потолков (ПТ6); ступени — зоной, кромка короба перед нишей — тонкой линией; в поле потолка: ПТ5 +5,650.

1000 мм · печать 1:1

Изм.	Кол.уч	Лист	№ док.	Подп.	Дата
Разраб.		Кырлан А.С.			04.11.26
Пров.					
ГИП					
Н. контр.					
Утв.					

ГД-2026-010-АИ

Дом 331 м²

Общая площадь 270,67* м² · * размеры приняты, не замерены (реестр — л. 8–10, К-1)

Дизайн-проект интерьера

Стадия	Лист	Листов
РП	197	216

Развёртка стены В. Спальня 4 (пом. 19)

М 1:25

Кырлан Александр Сергеевич

выпуск 04.11.2026 № 2a77323a49 · стр. 201 из 221

Привязки электроточек, стена В. Спальня 4 (пом. 19)

Спальня 4 (пом. 19) · вид изнутри помещения · привязки в мм, отметки в м · к развёртке на листе 197

ПРЕДВАРИТЕЛЬНО · не для производства работ · открыто пунктов: 15 (реестр — л. 8–10)

Развёртка стены В: электроточки и выводы

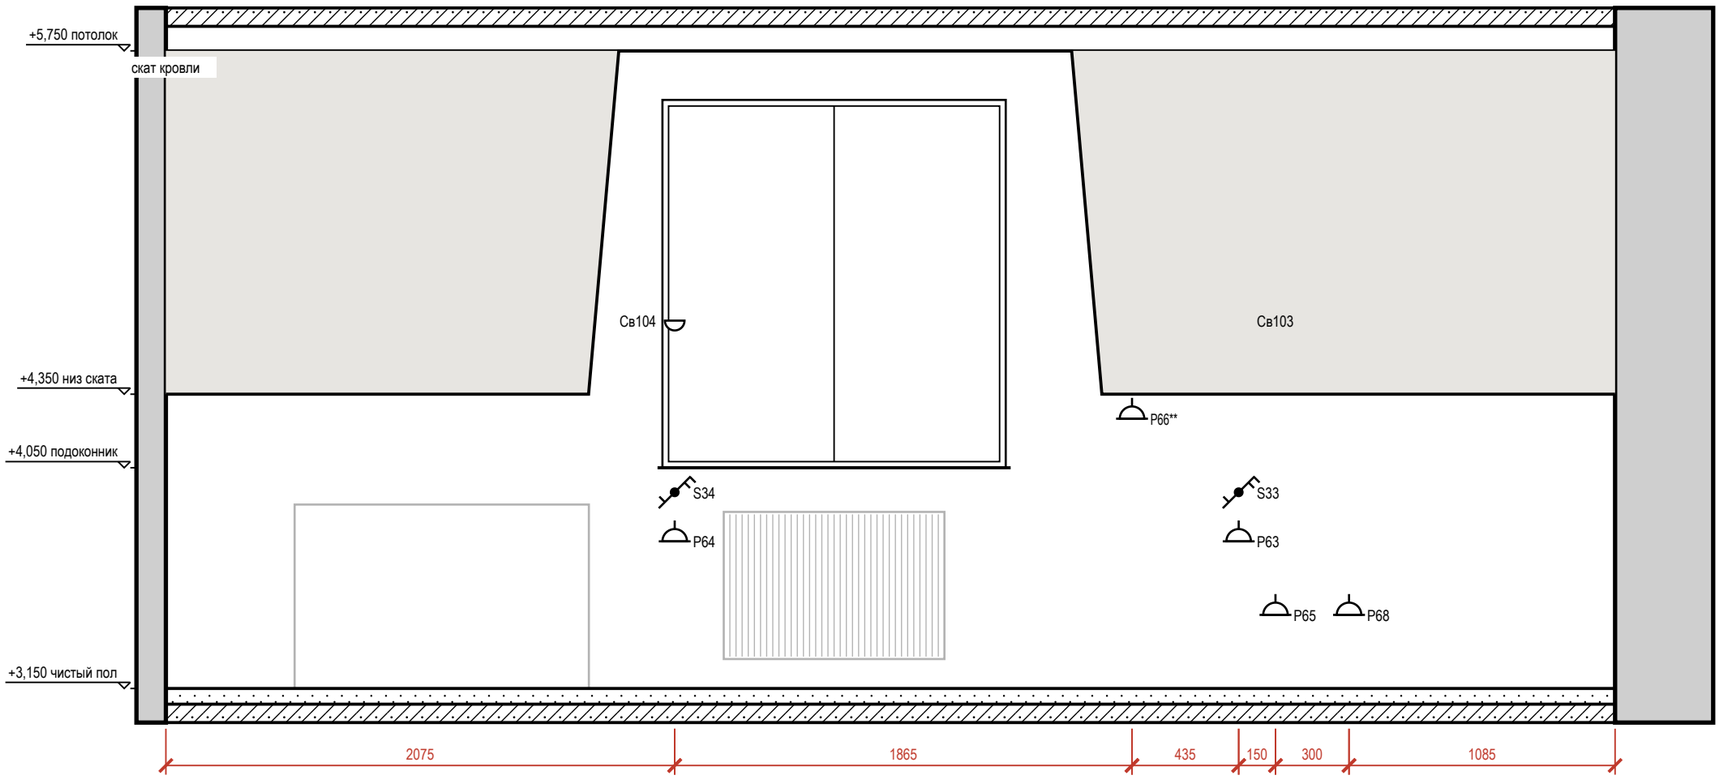


Таблица привязок электроточек и выводов

Марка	Назначение	От угла, мм	Н от пола, мм	Примечание
P64	розетка: у кровати	2075	600	гр. 19
S34	выключатель	2075	800	гр. 1
Св104	светильник настенный	2075	1500	гр. 1
P66**	розетка: ТВ над комодом (в одной зоне с ТВ5, LAN6)	3940	1100	гр. 19
P63	розетка: у кровати	4375	600	гр. 19

Марка	Назначение	От угла, мм	Н от пола, мм	Примечание
S33	выключатель	4375	800	гр. 1
Св103	светильник настенный	4375	1500	гр. 1
P65	розетка: у комода	4525	300	гр. 19
P68	розетка: уборка у входа	4825	300	гр. 19

Условные обозначения

- розетка с заземляющим контактом; у знака — марка, ×N постов в рамке, гр. — группа щита, Н — высота оси, мм
- выключатель одноклавишный
- выключатель двухклавишный (флажков — по числу клавиш)
- выключатель с проходной или перекрёстной клавишей (обратный флажок); тип клавиши — в подписи
- светильник настенный (бра), Н — высота оси
- привязки точек и выводов от угла и от пола, мм

Примечания

1. Вид «Привязки» стены В — электроточки и выводы ВК; архитектурная развёртка (мебель, отделка, проёмы, высоты) — на листе 197, расположение — на листе 128. Мебель и приборы — подложкой для ориентира; их марки и обозначения мебели, проёмов и стен — там же.
2. Привязки — в мм: по горизонтали от левого чистового угла стены до оси изделия, Н — от чистого пола до оси; все точки — в таблице привязок. Красная цепочка — привязки по осям; точки ближе 150 мм одна к другой в цепочку не дробятся — их привязки только в таблице.
3. У знака — марка электроточки (Р — розетка, S — выключатель, Св — светильник, ЭВ — вывод кабеля); посты в рамке и группа щита — в графе «Примечание»; группы по клавишам выключателя — на листе выключателей.

Допущения и предложения на листе

Основа листа: размеры и контуры этажей подобраны проектировщиком по составу помещений и площадям этажей с картинки 470 px (размеры на ней не читаются); обмер и исходный проект — задание (К-1); высоты: 1-й этаж 2800 мм, мансарда 2700 мм (горизонтальная часть) приняты; скаты кровли мансарды приняты по картинке: колено 1200 мм, уклон 45°, конёк вдоль длинной стороны; проект КР — задание (К-2); наружные стены 400 мм, перегородки 120 мм приняты (К-1); разрешённая мощность 15 кВт принята по типовым ТУ для частного дома (К-4); подрайон климата не задан — принят не северный (жилые от 2,5 м) (К-7).

Знак «*» — принято, не замерено и не подтверждено (замерить на объекте): К-2: отметка чистого пола этажа «Мансарда» +3,150 — принята без источника, все отметки мансарды считаются от неё.

Знак «**» — предложение проектировщика, заказчиком не утверждено (согласовать с заказчиком): Р66 — высота 1100 мм выше нормы 1 м (ПУЭ 6.6.30) по назначению: питание ТВ над комодом, в одной зоне с выводами ТВ5 и LAN6.

См. лист открытых вопросов (лист 8, записи К-1, К-2, К-4, К-7).

1000 мм · печать 1:1

Изм.	Кол.уч	Лист	№ док.	Подп.	Дата
Разраб.		Кырлан А.С.			04.11.26
Пров.					
ГИП					
Н. контр.					
Утв.					

ГД-2026-010-АИ

Дом 331 м²

Общая площадь 270,67* м² · * размеры приняты, не замерены (реестр — л. 8–10, К-1)

Дизайн-проект интерьера

Стадия	Лист	Листов
РП	198	216

Привязки электроточек, стена В. Спальня 4 (пом. 19)

М 1:25

Кырлан Александр Сергеевич


выпуск 04.11.2026 № 2a77323a49 · стр. 202 из 221

Развёртка стены Г. Спальня 4 (пом. 19)

Спальня 4 (пом. 19) · вид изнутри помещения · размеры в мм, отметки в м от ±0,000 (чистый пол 1-го этажа)

ПРЕДВАРИТЕЛЬНО · не для производства работ · открыто пунктов: 15 (реестр — л. 8–10)

Развёртка стены Г

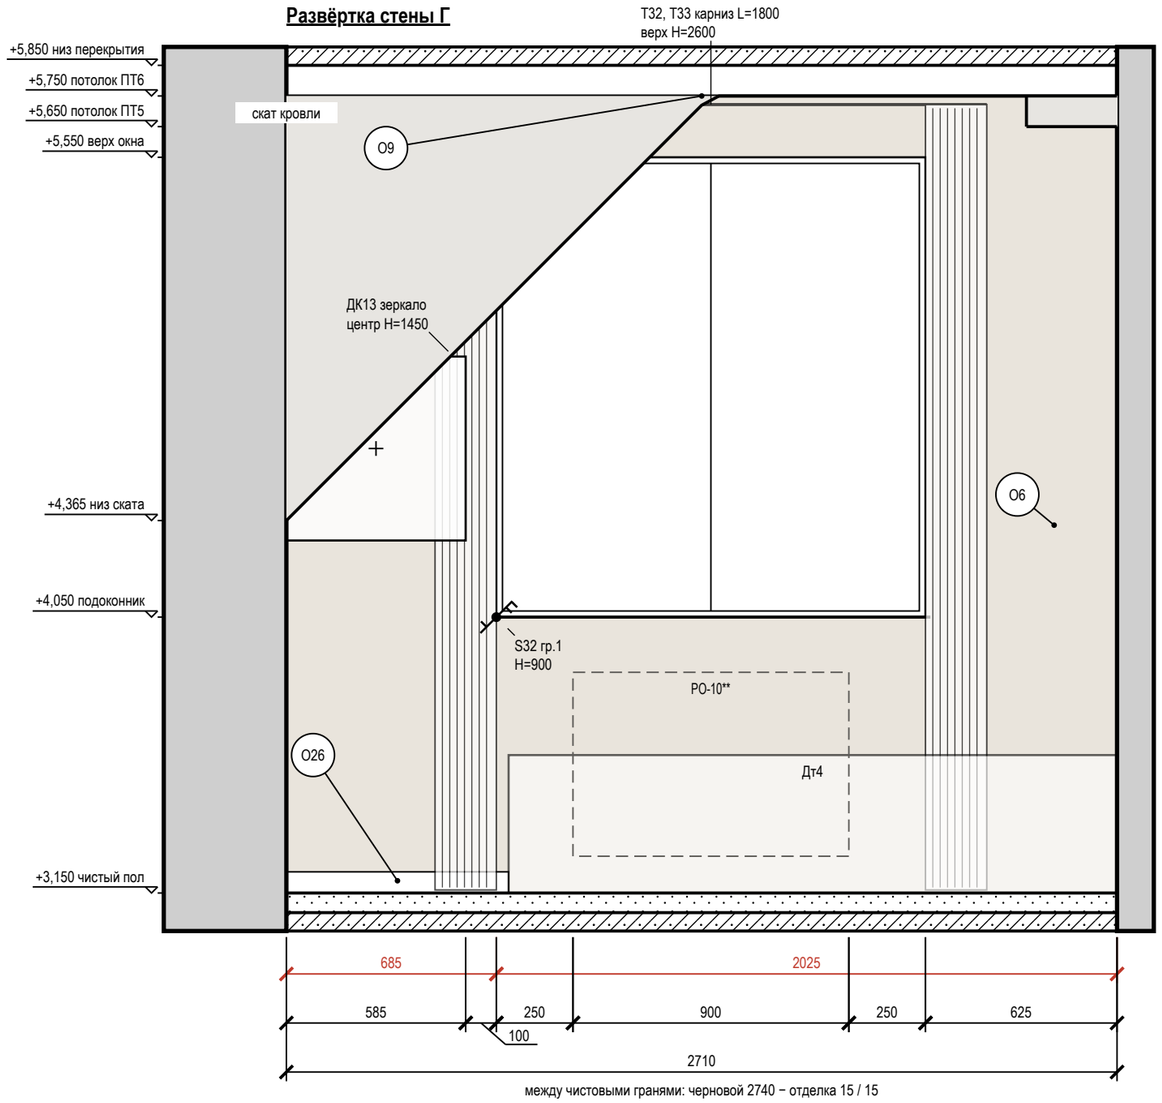

между чистовыми гранями: черновой 2740 − отделка 15 / 15


Допущения и предложения на листе. Основа листа: размеры и контуры этажей подобраны проектировщиком по составу помещений и площадям этажей с картинки 470 px (размеры на ней не читаются); обмер и исходный проект — задание (К-1); высоты: 1-й этаж 2800 мм, мансарда 2700 мм (горизонтальная часть) приняты; скаты кровли мансарды приняты по картинке: колено 1200 мм, уклон 45°, конёк вдоль длинной стороны; проект КР — задание (К-2); наружные стены 400 мм, перегородки 120 мм приняты (К-1); разрешённая мощность 15 кВт принята по типовым ТУ для частного дома (К-4); подрайон климата не задан — принят не северный (жилые от 2,5 м) (К-7). Знак «*» — принято, не замерено и не подтверждено (замерить на объекте): К-2: отметка чистого пола этажа «Мансарда» +3,150 — принята без источника, все отметки мансарды считаются от неё. Знак «**» — предложение проектировщика, заказчиком не утверждено (согласовать с заказчиком): К-11: РО-10 — прибор под окном по оси проёма, ширина ≈ 0,7 ширины окна — предложение ОВ (лист ОВ выводил его сам до, теперь он в данных — один источник для листа, мебели, DXF и IFC); котёл и мощность не выбраны (К-11) — размер по теплотехническому расчёту. См. лист открытых вопросов (лист 8, записи К-1, К-2, К-4, К-7; лист 9, запись К-11).

Примечания

1. Развёртки — вид на стену изнутри помещения, по часовой стрелке; расположение — на схеме листа и на листе 128; размеры — в мм по чистовым поверхностям; отметки — в м от ±0,000 (чистый пол 1-го этажа); высоты Н — от чистого пола помещения до оси изделия, у декора — до центра.
2. Красная цепочка — привязки электроточек и выводов по осям от угла чистовых стен; высота Н — у знака, от чистого пола до оси; высоты мебели, проёмов и границ отделки — колонкой отметок слева. Стена с 5 и более точками или с мелкими звеньями привязок показана двумя видами: архитектурная развёртка (мебель, отделка, проёмы, высоты) и вид «Привязки» на отдельном листе — точки и выводы с марками, одна цепочка по осям и таблица привязок (каждая точка — строка).
3. У знака электроточки: марка (Р — розетка, S — выключатель, Св — светильник, ЭВ — вывод кабеля), ×N — число постов в рамке, гр. — группа щита, Н — высота оси от чистого пола, мм; группы по клавишам выключателя — на листе выключателей.
4. Схема мебели, приборов и декора не является технической документацией для производства мебели; габариты — по паспортам изделий.
5. Картины и зеркала крепить к основанию по паспорту изделия (закладные и анкеры — в перечне скрытых работ); крест — ось центра предмета.
6. Карнизы (шины) — по ведомости текстиля декоратора: длина L и верх Н на развёртке — те же числа, что в ведомости; крепление — до окраски потолка.
7. Потолок — у каждой стены свой, по плану потолков (ПТ6, ПТ5); ступени — зоной, кромка короба перед нишей — тонкой линией.

1000 мм · печать 1:1

Схема развёрток (М 1:100)

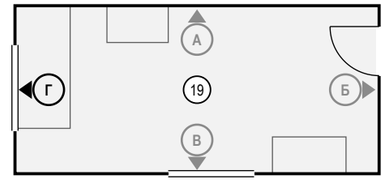

Условные обозначения

- выключатель одноклавишный
- выключатель двухклавишный (флажков — по числу клавиш)
- выключатель с проходной или перекрёстной клавишей (обратный флажок); тип клавиши — в подписи
- привязки точек и выводов от угла и от пола, мм
- мебель и приборы — фасад по расстановке (условно)
- зеркало: марка Д, крест — центр, Н — высота центра, мм
- карниз (шина) и шторы в собранном виде: марка Т, длина L, верх Н
- окно: проём, рама, подоконник
- радиатор отопления; марка — по плану отопления
- стены и перекрытия в сечении
- окраска: тон — цвет по коду производителя (условно)
- О1 — марка отделки по реестру отделки альбома
- А — марка развёртки: буква стены, стрелка — взгляд

Ведомость отделки (на листе)

Марка	Поверхность	Материал, изделие	Цвет, код	Кол.
О6	стены	окраска, Farrow & Ball Modern Emulsion, матовая, подготовка Q3	Farrow & Ball No. 226 «Joa's White»	4,9 м²
О9	потолок	окраска, Little Greene Absolute Matt, глубокоматовая, подготовка Q3	Little Greene No. 105 «Slaked Lime»	16,3 м²
О26	плинтус	плинтус МДФ, Orac Decor Contour (Luxxus), h 69 мм, SX165	Farrow & Ball No. 226 «Joa's White»	0,7 м

Изм.	Кол.уч	Лист	№ док.	Подп.	Дата
Разраб.		Кырлан А.С.			04.11.26
Пров.					
ГИП					
Н. контр.					
Утв.					

ГД-2026-010-АИ

Дом 331 м²

Общая площадь 270,67* м² · * размеры приняты, не замерены (реестр — л. 8–10, К-1)

Дизайн-проект интерьера

Стадия	Лист	Листов
РП	199	216

Развёртка стены Г. Спальня 4 (пом. 19)

М 1:20

Кырлан Александр Сергеевич


выпуск 04.11.2026 № 2a77323a49 · стр. 203 из 221

Развёртки стен А, Б. Санузел 2 (пом. 20)

Санузел 2 (пом. 20) · вид изнутри помещения · размеры в мм, отметки в м от ±0,000 (чистый пол 1-го этажа)


ПРЕДВАРИТЕЛЬНО · не для производства работ · открыто пунктов: 15 (реестр — л. 8–10)

Развёртка стены А

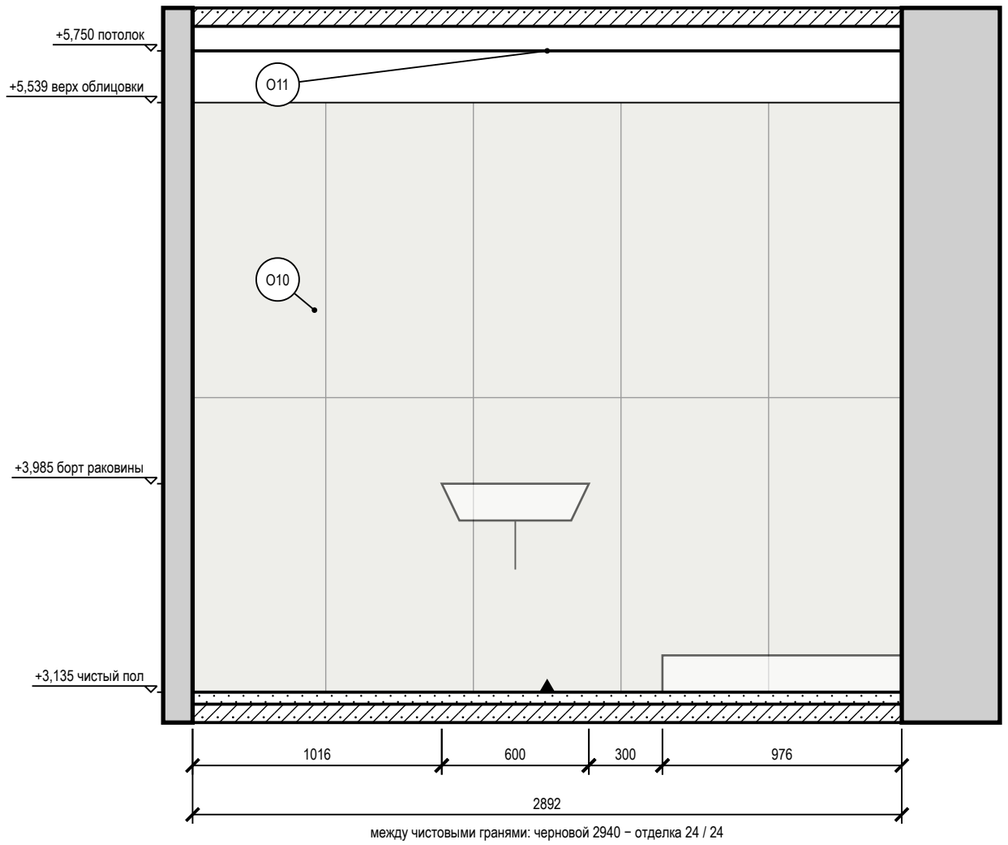


между чистовыми гранями: черновой 2940 − отделка 24 / 24

Развёртка стены Б

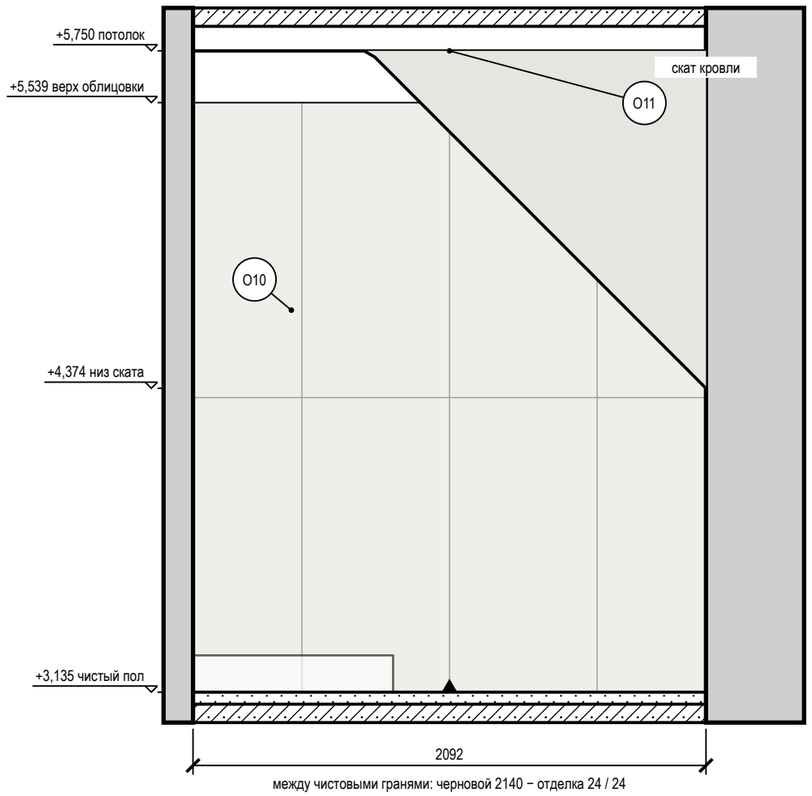

между чистовыми гранями: черновой 2140 − отделка 24 / 24

Схема развёрток (М 1:100)

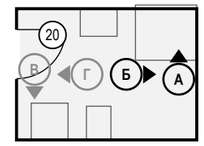

Условные обозначения

- мебель и приборы — фасад по расстановке (условно)
- стены и перекрытия в сечении
- плитка: сетка швов по формату, ▲ — ось старта
- О1 — марка отделки по реестру отделки альбома
- А — марка развёртки: буква стены, стрелка — взгляд

Ведомость отделки (на листе)

Марка	Поверхность	Материал, изделие	Цвет, код	Кол.
О10	стены	облицовка плиткой, Atlas Concorde Marvel Travertine, 600×1200×9 мм, A8UZ, затирка CG2WA	Atlas Concorde A8UZ «Marvel Travertine»	12 м²
О11	потолок	окраска, Little Greene Intelligent Bathroom, матовая, подготовка Q3	Little Greene No. 105 «Slaked Lime»	6,3 м²

Допущения и предложения на листе

Основа листа: размеры и контуры этажей подобраны проектировщиком по составу помещений и площадям этажей с картинки 470 px (размеры на ней не читаются); обмер и исходный проект — задание (К-1); высоты: 1-й этаж 2800 мм, мансарда 2700 мм (горизонтальная часть) приняты; скаты кровли мансарды приняты по картинке: колено 1200 мм, уклон 45°, конёк вдоль длинной стороны; проект КР — задание (К-2); наружные стены 400 мм, перегородки 120 мм приняты (К-1); разрешённая мощность 15 кВт принята по типовым ТУ для частного дома (К-4); подрайон климата не задан — принят не северный (жилые от 2,5 м) (К-7).

Знак «*» — принято, не замерено и не подтверждено (замерить на объекте): К-2: отметка чистого пола этажа «Мансарда» +3,150 — принята без источника, все отметки мансарды считаются от неё. См. лист открытых вопросов (лист 8, записи К-1, К-2, К-4, К-7).

Примечания

1. Развёртки — вид на стену изнутри помещения, по часовой стрелке; расположение — на схеме листа и на листе 128; размеры — в мм по чистовым поверхностям; отметки — в м от ±0,000 (чистый пол 1-го этажа); высоты Н — от чистого пола помещения до оси изделия, у декора — до центра.
2. Стены А, Б показаны двумя видами: здесь — архитектурная развёртка (мебель, отделка, проёмы, высоты), электроточки и выводы ВК с привязками и таблицей — на листах 201, 202 («Привязки»).
3. Схема мебели, приборов и декора не является технической документацией для производства мебели; габариты — по паспортам изделий (* — высота не задана в проекте, показана по типовому изделию).
4. Облицовка — по сетке швов 2 мм, раскладка от оси стены (треугольник у пола), целые ряды от пола; подрезки — по листу раскладки плитки.
5. Гидроизоляция в 2 слоя, заход на стены 200 мм; у душа — до 2000 и 500 мм за поддон — до облицовки, с актом скрытых работ и тестом проливом (узел — на листе узлов).

1000 мм · печать 1:1

Изм.	Кол.уч	Лист	№ док.	Подп.	Дата
Разраб.		Кырлан А.С.			04.11.26
Пров.					
ГИП					
Н. контр.					
Утв.					

ГД-2026-010-АИ

Дом 331 м²

Общая площадь 270,67* м² · * размеры приняты, не замерены (реестр — л. 8–10, К-1)

Дизайн-проект интерьера

Стадия	Лист	Листов
РП	200	216

Развёртки стен А, Б. Санузел 2 (пом. 20)

М 1:25

Кырлан Александр Сергеевич

выпуск 04.11.2026 № 2a77323a49 · стр. 204 из 221

Привязки электроточек и выводов ВК, стена А. Санузел 2 (пом. 20)

Санузел 2 (пом. 20) · вид изнутри помещения · привязки в мм, отметки в м · к развёртке на листе 200

ПРЕДВАРИТЕЛЬНО · не для производства работ · открыто пунктов: 15 (реестр — л. 8–10)

Развёртка стены А: электроточки и выводы

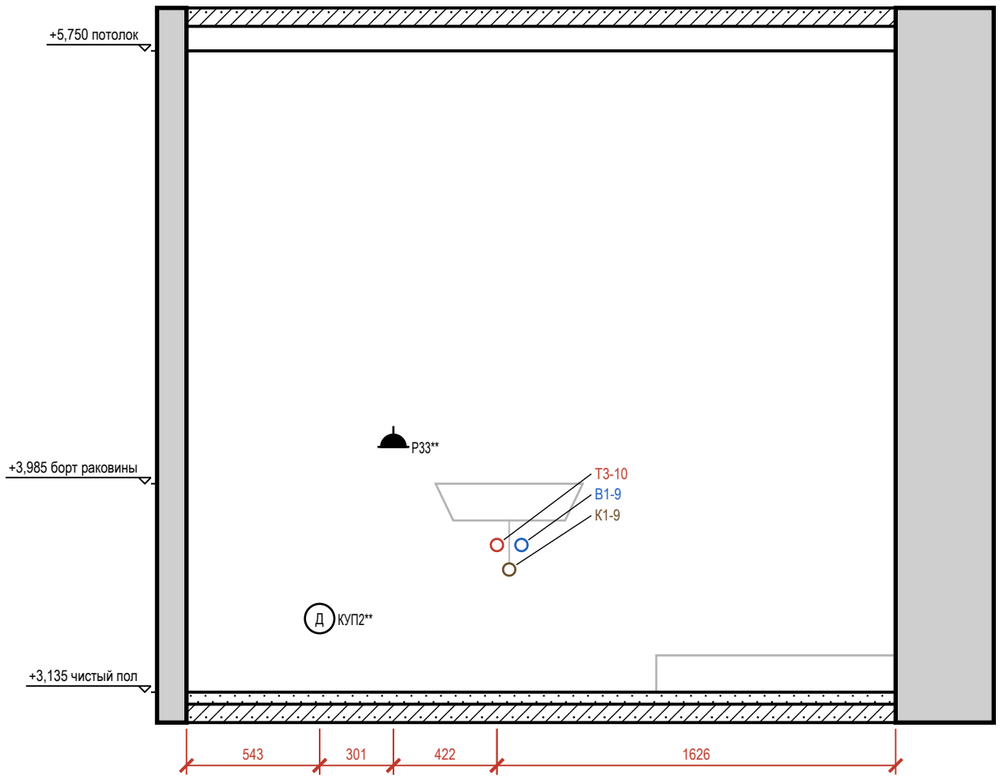



Таблица привязок электроточек и выводов

Марка	Назначение	От угла, мм	Н от пола, мм	Примечание
КУП2**	КУП — уравнивание потенциалов (ДСУП)	543	300	
Р33**	розетка: фен у умывальника	844	1000	гр. 13, IP44
Т3-10	горячая вода — умывальник	1266	600*	межос. 100
К1-9	канализация — умывальник	1316	500*	Ø50
В1-9	холодная вода — умывальник	1366	600*	межос. 100

Условные обозначения

- розетка влагозащищённая IP44
- вывод В1 (код — в ведомости привязок)
- вывод Т3 (код — в ведомости привязок)
- вывод К1 (код — в ведомости привязок)
- привязки точек и выводов от угла и от пола, мм
- А — марка развёртки: буква стены, стрелка — взгляд

Схема развёрток (М 1:50)

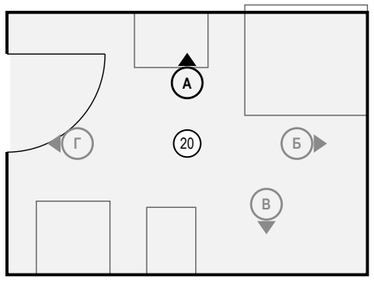

Примечания

1. Вид «Привязки» стены А — электроточки и выводы ВК; архитектурная развёртка (мебель, отделка, проёмы, высоты) — на листе 200, расположение — на листе 128. Мебель и приборы — подложкой для ориентира; их марки и обозначения мебели, проёмов и стен — там же.
2. Привязки — в мм: по горизонтали от левого чистового угла стены до оси изделия, Н — от чистого пола до оси; все точки — в таблице привязок. Красная цепочка — привязки по осям; точки ближе 150 мм одна к другой в цепочку не дробятся — их привязки только в таблице.
3. У знака — марка электроточки (Р — розетка, S — выключатель, Св — светильник, ЭВ — вывод кабеля); посты в рамке и группа щита — в графе «Примечание»; группы по клавишам выключателя — на листе выключателей.
4. Коды выводов ВК: В1 — холодная вода, Т3 — горячая вода, К1 — канализация; номер после дефиса — номер вывода на листе выводов сантехники; * — высота принята по типовой практике монтажа, окончательно — по паспорту прибора.

Допущения и предложения на листе

Основа листа: размеры и контуры этажей подобраны проектировщиком по составу помещений и площадям этажей с картинки 470 px (размеры на ней не читаются); обмер и исходный проект — задание (К-1); высоты: 1-й этаж 2800 мм, мансарда 2700 мм (горизонтальная часть) приняты; скаты кровли мансарды приняты по картинке: колено 1200 мм, уклон 45°, конёк вдоль длинной стороны; проект КР — задание (К-2); наружные стены 400 мм, перегородки 120 мм приняты (К-1); разрешённая мощность 15 кВт принята по типовым ТУ для частного дома (К-4); подрайон климата не задан — принят не северный (жилые от 2,5 м) (К-7).

Знак «*» — принято, не замерено и не подтверждено (замерить на объекте): К-2: отметка чистого пола этажа «Мансарда» +3,150 — принята без источника, все отметки мансарды считаются от неё.

Знак «**» — предложение проектировщика, заказчиком не утверждено (согласовать с заказчиком): Р33 — по образцу: Розетка Р33 на высоте 1100 мм, вне шва плитки; КУП2 — по образцу: Добавлены выводы к вентиляторам: ЭВ4 (ВР1, ванная) и ЭВ5 (ВР3, санузел 2) — группа 3, высота 2389 мм, включение с основным светом, таймер выбега в вентиляторе; и коробки уравнивания потенциалов КУП1 (ванная) и КУП2 (санузел 2) — высота 300 мм, у входа, вне зон 0–2, проводник от шины РЕ щита ЩК …; сдвиг под раскладку плитки стены А на 27 мм вдоль стены — ось на шве или в центре плитки, привязка по таблице листа.

См. лист открытых вопросов (лист 8, записи К-1, К-2, К-4, К-7).

1000 мм · печать 1:1

Изм.	Кол.уч	Лист	№ док.	Подп.	Дата
Разраб.		Кырлан А.С.			04.11.26
Пров.					
ГИП					
Н. контр.					
Утв.					

ГД-2026-010-АИ

Дом 331 м²

Общая площадь 270,67* м² · * размеры приняты, не замерены (реестр — л. 8–10, К-1)

Дизайн-проект интерьера	Стадия	Лист	Листов
	РП	201	216

Привязки электроточек и выводов ВК, стена А. Санузел 2 (пом. 20)

М 1:25

Кырлан Александр Сергеевич

выпуск 04.11.2026 № 2a77323a49 · стр. 205 из 221

Привязки электроточек и выводов ВК, стена Б. Санузел 2 (пом. 20)

Санузел 2 (пом. 20) · вид изнутри помещения · привязки в мм, отметки в м · к развёртке на листе 200

ПРЕДВАРИТЕЛЬНО · не для производства работ · открыто пунктов: 15 (реестр — л. 8–10)

Развёртка стены Б: электроточки и выводы

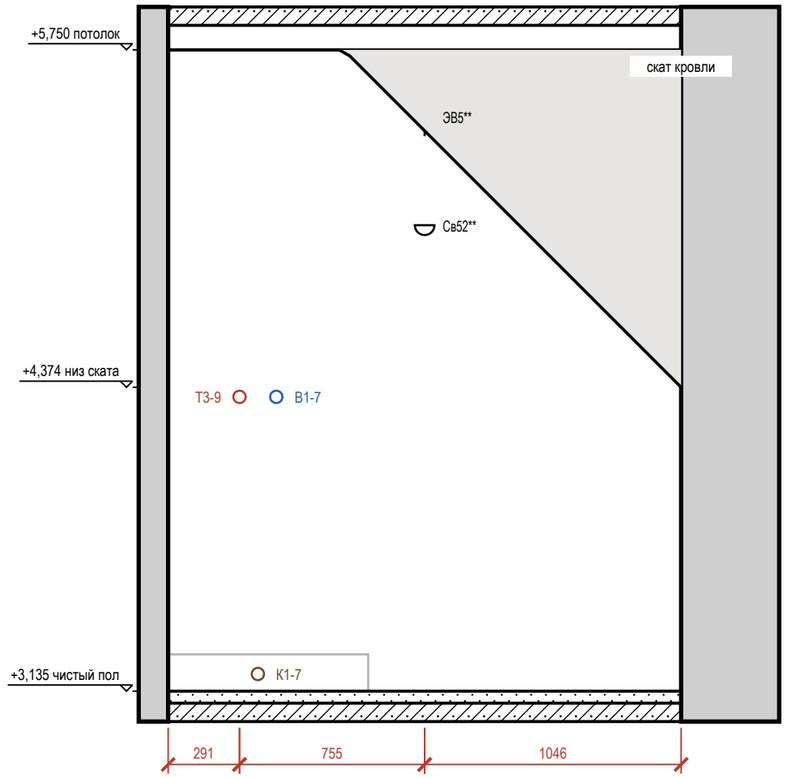



Таблица привязок электроточек и выводов

Марка	Назначение	От угла, мм	Н от пола, мм	Примечание
Т3-9	горячая вода — душ	291	1200*	межос. 150
К1-7	канализация — душ	366	70*	Ø50; сифон поддона
В1-7	холодная вода — душ	441	1200*	межос. 150
Св52**	светильник настенный	1046	1900	гр. 3
ЭВ5**	вывод кабеля: вентилятор ВР3 (таймер выбега)	1046	2343	гр. 3

Условные обозначения

- вывод кабеля для подключения прибора (без розетки), марка ЭВ
- светильник настенный (бра), Н — высота оси
- вывод В1 (код — в ведомости привязок)
- вывод Т3 (код — в ведомости привязок)
- вывод К1 (код — в ведомости привязок)
- привязки точек и выводов от угла и от пола, мм
- марка развёртки: буква стены, стрелка — взгляд

Схема развёрток (М 1:50)

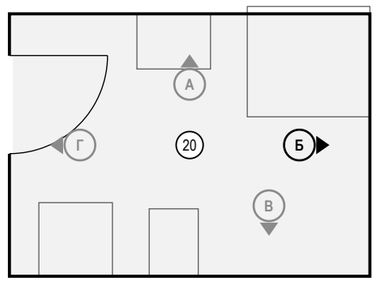

Примечания

1. Вид «Привязки» стены Б — электроточки и выводы ВК; архитектурная развёртка (мебель, отделка, проёмы, высоты) — на листе 200, расположение — на листе 128. Мебель и приборы — подложкой для ориентира; их марки и обозначения мебели, проёмов и стен — там же.
2. Привязки — в мм: по горизонтали от левого чистового угла стены до оси изделия, Н — от чистого пола до оси; все точки — в таблице привязок. Красная цепочка — привязки по осям; точки ближе 150 мм одна к другой в цепочку не дробятся — их привязки только в таблице.
3. У знака — марка электроточки (Р — розетка, S — выключатель, Св — светильник, ЭВ — вывод кабеля); посты в рамке и группа щита — в графе «Примечание»; группы по клавишам выключателя — на листе выключателей.
4. Коды выводов ВК: В1 — холодная вода, Т3 — горячая вода, К1 — канализация; номер после дефиса — номер вывода на листе выводов сантехники; * — высота принята по типовой практике монтажа, окончательно — по паспорту прибора.

Допущения и предложения на листе

Основа листа: размеры и контуры этажей подобраны проектировщиком по составу помещений и площадям этажей с картинки 470 px (размеры на ней не читаются); обмер и исходный проект — задание (К-1); высоты: 1-й этаж 2800 мм, мансарда 2700 мм (горизонтальная часть) приняты; скаты кровли мансарды приняты по картинке: колено 1200 мм, уклон 45°, конёк вдоль длинной стороны; проект КР — задание (К-2); наружные стены 400 мм, перегородки 120 мм приняты (К-1); разрешённая мощность 15 кВт принята по типовым ТУ для частного дома (К-4); подрайон климата не задан — принят не северный (жилые от 2,5 м) (К-7).

Знак «*» — принято, не замерено и не подтверждено (замерить на объекте): К-2: отметка чистого пола этажа «Мансарда» +3,150 — принята без источника, все отметки мансарды считаются от неё.

Знак «**» — предложение проектировщика, заказчиком не утверждено (согласовать с заказчиком): ИЗ-1: Св52 — Сдвиг под раскладку плитки стены Б на 25 мм вдоль стены — ось на шве или в центре плитки, привязка по таблице листа; ЭВ5 — по образцу: Добавлены выводы к вентиляторам: ЭВ4 (ВР1, ванная) и ЭВ5 (ВР3, санузел 2) — группа 3, высота 2389 мм, включение с основным светом, таймер выбега в вентиляторе; и коробки уравнивания потенциалов КУП1 (ванная) и КУП2 (санузел 2) — высота 300 мм, у входа, вне зон 0–2, проводник от шины РЕ щита ЩК …; сдвиг под раскладку плитки стены Б на 75 мм вдоль стены и на 46 мм ниже — ось на шве или в центре плитки, привязка по таблице листа.

См. лист открытых вопросов (лист 8, записи К-1, К-2, К-4, К-7; лист 10, запись ИЗ-1).

1000 мм · печать 1:1

Изм.	Кол.уч	Лист	№ док.	Подп.	Дата
Разраб.		Кырлан А.С.			04.11.26
Пров.					
ГИП					
Н. контр.					
Утв.					

ГД-2026-010-АИ

Дом 331 м²

Общая площадь 270,67* м² · * размеры приняты, не замерены (реестр — л. 8–10, К-1)

Дизайн-проект интерьера	Стадия	Лист	Листов
	РП	202	216

Привязки электроточек и выводов ВК, стена Б. Санузел 2 (пом. 20)

М 1:25

Кырлан Александр Сергеевич


выпуск 04.11.2026 · 2a77323a49 · стр. 206 из 221

Развёртки стен В, Г. Санузел 2 (пом. 20)

Санузел 2 (пом. 20) · вид изнутри помещения · размеры в мм, отметки в м от ±0,000 (чистый пол 1-го этажа)


ПРЕДВАРИТЕЛЬНО · не для производства работ · открыто пунктов: 15 (реестр — л. 8–10)

Развёртка стены В

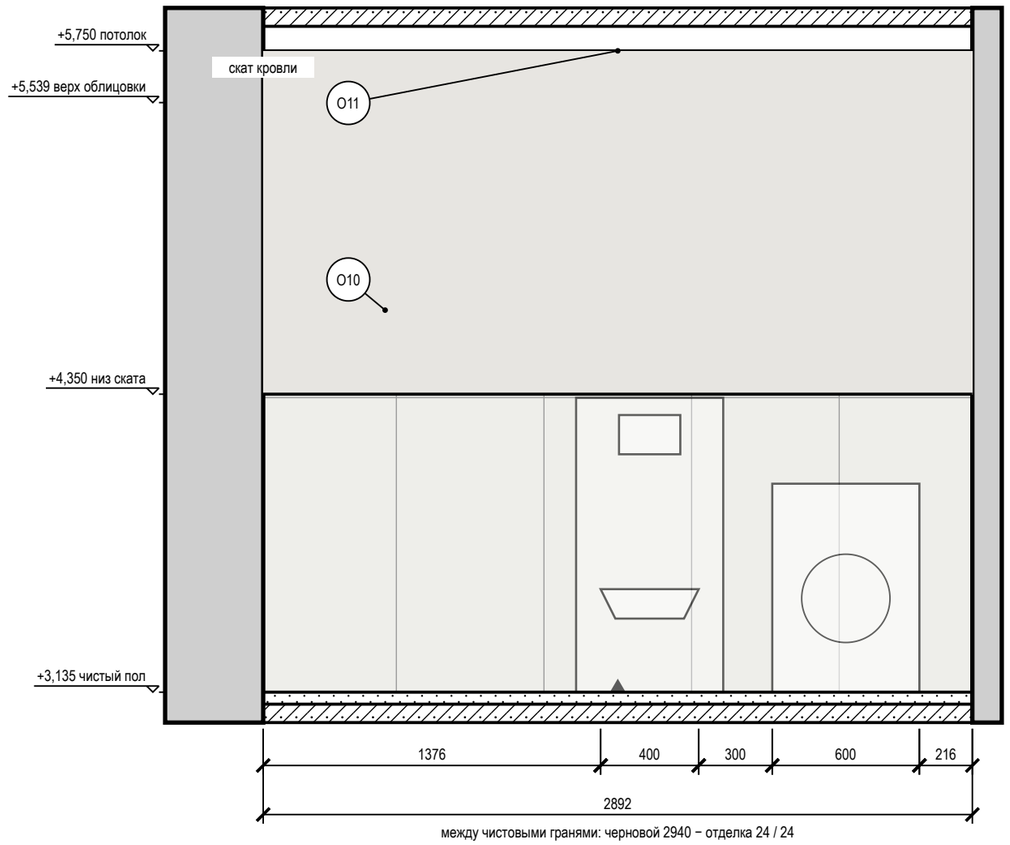


между чистовыми гранями: черновой 2940 − отделка 24 / 24

Развёртка стены Г

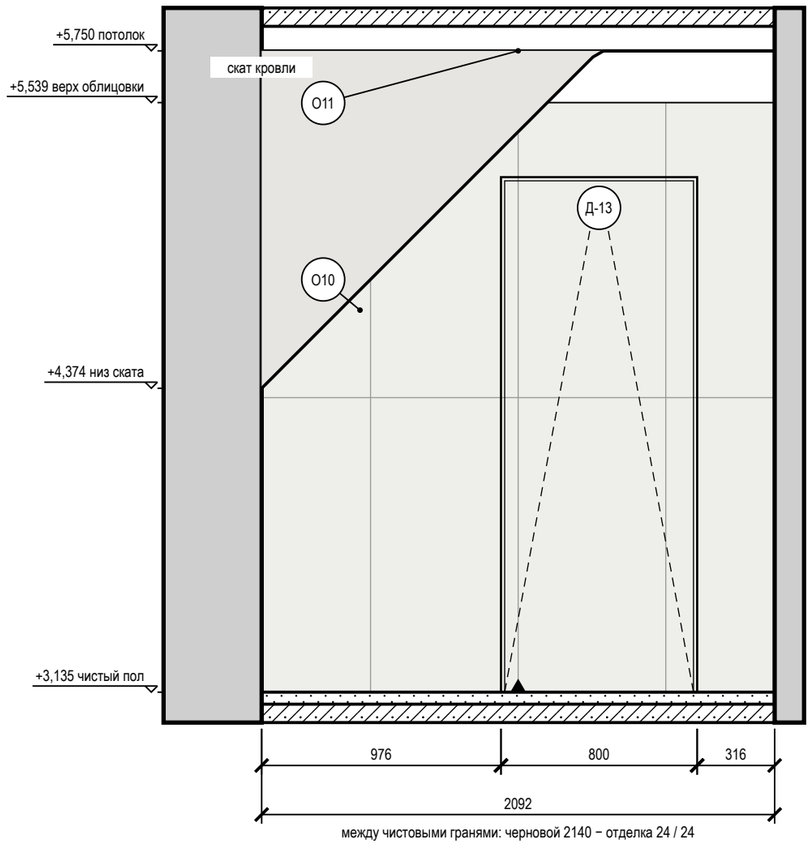

между чистовыми гранями: черновой 2140 − отделка 24 / 24

Схема развёрток (М 1:100)

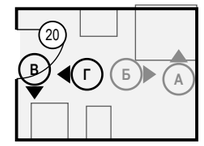

Условные обозначения

- мебель и приборы — фасад по расстановке (условно)
- дверь скрытого монтажа: полотно в плоскости стены (узел — на листе узлов)
- стены и перекрытия в сечении
- плитка: сетка швов по формату, ▲ — ось старта
- О1 — марка отделки по реестру отделки альбома
- А — марка развёртки: буква стены, стрелка — взгляд

Ведомость отделки (на листе)

Марка	Поверхность	Материал, изделие	Цвет, код	Кол.
О10	стены	облицовка плиткой, Atlas Concorde Marvel Travertine, 600×1200×9 мм, A8UZ, затирка CG2WA	Atlas Concorde A8UZ «Marvel Travertine»	10,3 м²
О11	потолок	окраска, Little Greene Intelligent Bathroom, матовая, подготовка Q3	Little Greene No. 105 «Slaked Lime»	6,3 м²

Допущения и предложения на листе

Основа листа: размеры и контуры этажей подобраны проектировщиком по составу помещений и площадям этажей с картинки 470 px (размеры на ней не читаются); обмер и исходный проект — задание (К-1); высоты: 1-й этаж 2800 мм, мансарда 2700 мм (горизонтальная часть) приняты; скаты кровли мансарды приняты по картинке: колено 1200 мм, уклон 45°, конёк вдоль длинной стороны; проект КР — задание (К-2); наружные стены 400 мм, перегородки 120 мм приняты (К-1); разрешённая мощность 15 кВт принята по типовым ТУ для частного дома (К-4); подрайон климата не задан — принят не северный (жилые от 2,5 м) (К-7).

Знак «*» — принято, не замерено и не подтверждено (замерить на объекте): К-2: отметка чистого пола этажа «Мансарда» +3,150 — принята без источника, все отметки мансарды считаются от неё. См. лист открытых вопросов (лист 8, записи К-1, К-2, К-4, К-7).

Примечания

1. Развёртки — вид на стену изнутри помещения, по часовой стрелке; расположение — на схеме листа и на листе 128; размеры — в мм по чистовым поверхностям; отметки — в м от ±0,000 (чистый пол 1-го этажа); высоты Н — от чистого пола помещения до оси изделия, у декора — до центра.
2. Стена В показана двумя видами: здесь — архитектурная развёртка (мебель, отделка, проёмы, высоты), электроточки и выводы ВК с привязками и таблицей — на листе 204 («Привязки»).
3. Схема мебели, приборов и декора не является технической документацией для производства мебели; габариты — по паспортам изделий (* — высота не задана в проекте, показана по типовому изделию).
4. Облицовка — по сетке швов 2 мм, раскладка от оси стены (треугольник у пола), целые ряды от пола; подрезки — по листу раскладки плитки.
5. Гидроизоляция в 2 слоя, заход на стены 200 мм; у душа — до 2000 и 500 мм за поддон — до облицовки, с актом скрытых работ и тестом проливом (узел — на листе узлов).
6. Двери скрытого монтажа — полотно в плоскости стены, отделка стены по полотну, плинтус прерывается у короба (узел — на листе узлов).

1000 мм · печать 1:1

Изм.	Кол.уч	Лист	№ док.	Подп.	Дата
Разраб.		Кырлан А.С.			04.11.26
Пров.					
ГИП					
Н. контр.					
Утв.					

ГД-2026-010-АИ

Дом 331 м²

Общая площадь 270,67* м² · * размеры приняты, не замерены (реестр — л. 8–10, К-1)

Дизайн-проект интерьера

Стадия	Лист	Листов
РП	203	216

Развёртки стен В, Г. Санузел 2 (пом. 20)

М 1:25

Кырлан Александр Сергеевич

выпуск 04.11.2026 № 2a77323a49 · стр. 207 из 221

Привязки электроточек и выводов ВК, стена В. Санузел 2 (пом. 20)

Санузел 2 (пом. 20) · вид изнутри помещения · привязки в мм, отметки в м · к развёртке на листе 203

ПРЕДВАРИТЕЛЬНО · не для производства работ · открыто пунктов: 15 (реестр — л. 8–10)

Развёртка стены В: электроточки и выводы

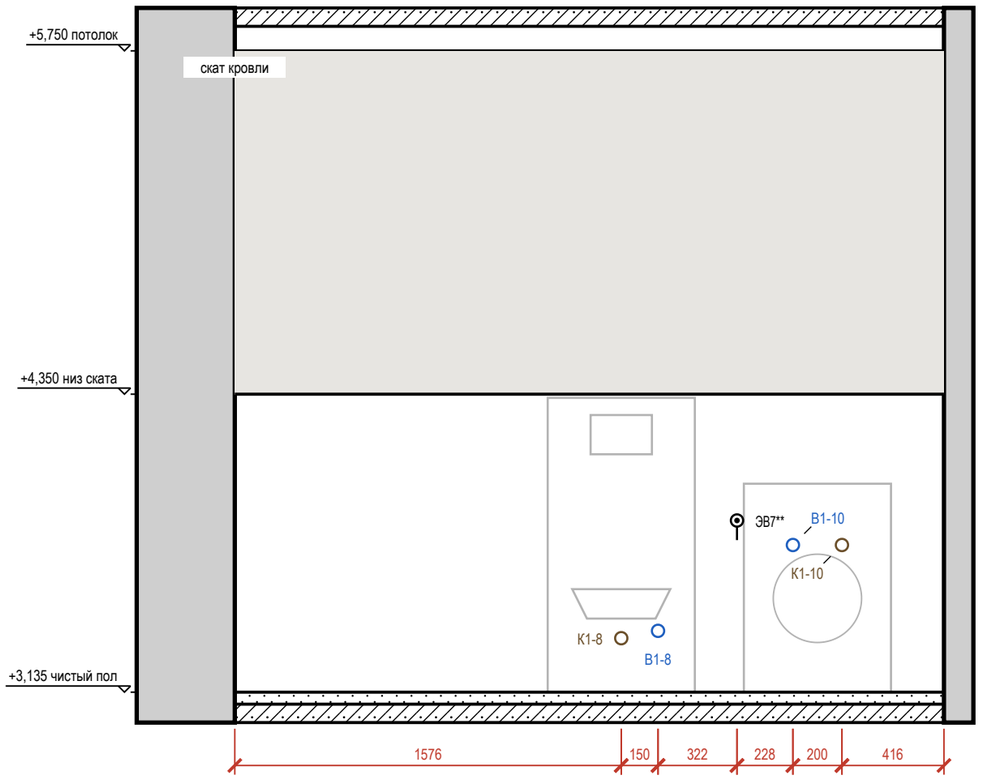



Таблица привязок электроточек и выводов

Марка	Назначение	От угла, мм	Н от пола, мм	Примечание
К1-8	канализация — унитаз подвесной	1576	220*	Ø110
В1-8	холодная вода — унитаз подвесной	1726	250*	в раме инсталляции
ЭВ7**	вывод кабеля: полотенцесушитель П13	2048	700	гр. 13
В1-10	холодная вода — стиральная машина	2276	600*	кран машины
К1-10	канализация — стиральная машина	2476	600*	Ø50

Условные обозначения

- вывод кабеля для подключения прибора (без розетки), марка ЭВ
- вывод В1 (код — в ведомости привязок)
- вывод К1 (код — в ведомости привязок)
- привязки точек и выводов от угла и от пола, мм
- марка развёртки: буква стены, стрелка — взгляд

Схема развёрток (М 1:50)

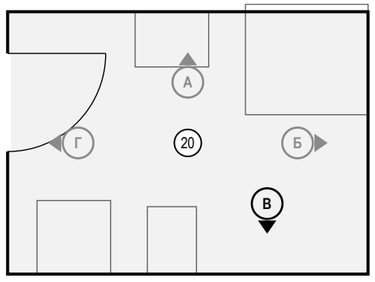

Примечания

1. Вид «Привязки» стены В — электроточки и выводы ВК; архитектурная развёртка (мебель, отделка, проёмы, высоты) — на листе 203, расположение — на листе 128. Мебель и приборы — подложкой для ориентира; их марки и обозначения мебели, проёмов и стен — там же.
2. Привязки — в мм: по горизонтали от левого чистового угла стены до оси изделия, Н — от чистого пола до оси; все точки — в таблице привязок. Красная цепочка — привязки по осям; точки ближе 150 мм одна к другой в цепочку не дробятся — их привязки только в таблице.
3. У знака — марка электроточки (Р — розетка, S — выключатель, Св — светильник, ЭВ — вывод кабеля); посты в рамке и группа щита — в графе «Примечание»; группы по клавишам выключателя — на листе выключателей.
4. Коды выводов ВК: В1 — холодная вода, Т3 — горячая вода, К1 — канализация; номер после дефиса — номер вывода на листе выводов сантехники; * — высота принята по типовой практике монтажа, окончательно — по паспорту прибора.

Допущения и предложения на листе

Основа листа: размеры и контуры этажей подобраны проектировщиком по составу помещений и площадям этажей с картинки 470 px (размеры на ней не читаются); обмер и исходный проект — задание (К-1); высоты: 1-й этаж 2800 мм, мансарда 2700 мм (горизонтальная часть) приняты; скаты кровли мансарды приняты по картинке: колено 1200 мм, уклон 45°, конёк вдоль длинной стороны; проект КР — задание (К-2); наружные стены 400 мм, перегородки 120 мм приняты (К-1); разрешённая мощность 15 кВт принята по типовым ТУ для частного дома (К-4); подрайон климата не задан — принят не северный (жилые от 2,5 м) (К-7).

Знак «*» — принято, не замерено и не подтверждено (замерить на объекте): К-2: отметка чистого пола этажа «Мансарда» +3,150 — принята без источника, все отметки мансарды считаются от неё.

Знак «**» — предложение проектировщика, заказчиком не утверждено (согласовать с заказчиком): ЭВ7 — по образцу: Добавлены электрические полотенцесушители IP44: П10 в ванной (480 мм, низ 900 мм) и П13 в санузле 2 (400 мм, низ 900 мм), выводы ЭВ6 и ЭВ7; мощность группы 13 — 2,4 кВт вместо 1,8 кВт; сдвиг под раскладку плитки стены В на 72 мм вдоль стены — ось на шве или в центре плитки, привязка по таблице листа.

См. лист открытых вопросов (лист 8, записи К-1, К-2, К-4, К-7).

1000 мм · печать 1:1

Изм.	Кол.уч	Лист	№ док.	Подп.	Дата
Разраб.		Кырлан А.С.			04.11.26
Пров.					
ГИП					
Н. контр.					
Утв.					

ГД-2026-010-АИ

Дом 331 м²

Общая площадь 270,67* м² · * размеры приняты, не замерены (реестр — л. 8–10, К-1)

Дизайн-проект интерьера

Стадия	Лист	Листов
РП	204	216

Привязки электроточек и выводов ВК, стена В. Санузел 2 (пом. 20)

М 1:25

Кырлан Александр Сергеевич


выпуск 04.11.2026 № 2a77323a49 · стр. 208 из 221

Узлы. Лист 1 из 2

Пороги и стыки покрытий, скрытые двери, короба стояков, гидроизоляция, плинтус


1 Порог 15 мм: мокрая зона — смежное помещение (М 1:5)

Применение: двери Д-2, Д-9, Д-13; места — листы 127, 128

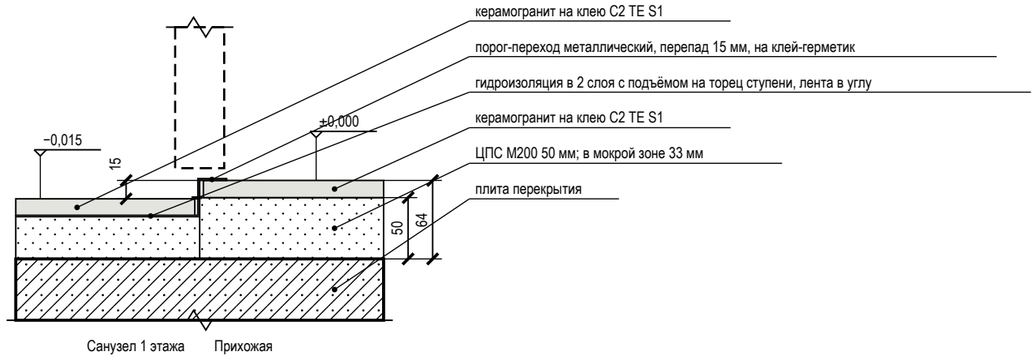


2 Стык покрытий пола с перепадом 30 мм, профиль-переход (М 1:5)

Применение: проёмы 5↔11; места — лист 127

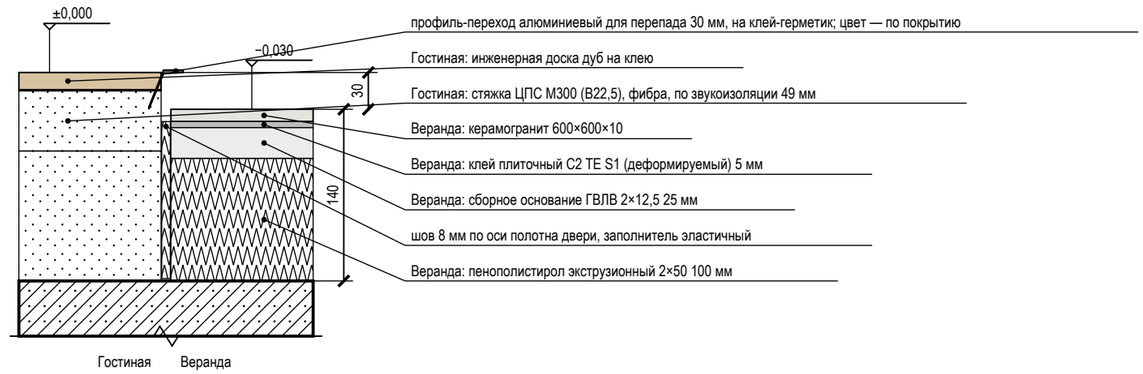


3 Дверь скрытого монтажа в плоскости стены, плинтус (М 1:5)

Применение: двери Д-1, Д-2, Д-7, Д-8, Д-9, Д-10, Д-11, Д-12, Д-13; места — листы 127, 128

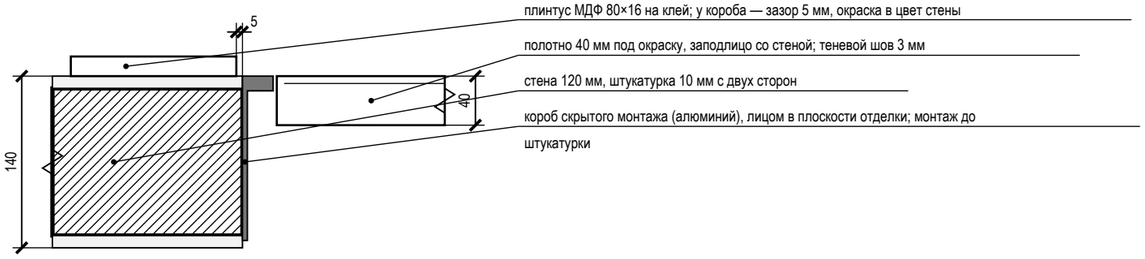

4 Короб стояков К1-1 с люком и звукоизоляцией (М 1:10)

Применение: пом. 3, 1, 8; места — лист 127

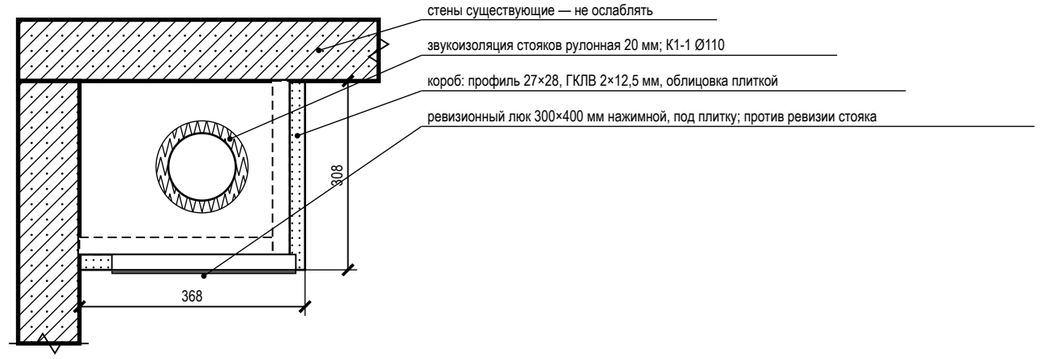

Допущения и предложения на листе

Основа листа: размеры и контуры этажей подобраны проектировщиком по составу помещений и площадям этажей с картинки 470 px (размеры на ней не читаются); обмер и исходный проект — задание (К-1); высоты: 1-й этаж 2800 мм, мансарда 2700 мм (горизонтальная часть) приняты; скаты кровли мансарды приняты по картинке: колено 1200 мм, уклон 45°, конёк вдоль длинной стороны; проект КР — задание (К-2); наружные стены 400 мм, перегородки 120 мм приняты (К-1); разрешённая мощность 15 кВт принята по типовым ТУ для частного дома (К-4); подрайон климата не задан — принят не северный (жилые от 2,5 м) (К-7).

См. лист открытых вопросов (лист 8, записи К-1, К-2, К-4, К-7).

Условные обозначения

- железобетон (плита, стены) — условно: конструкция не установлена
- кладка, перегородка — условно: конструкция не установлена
- стяжка, раствор
- гипсокартон ГКЛВ
- звукоизоляция, эластичный заполнитель
- плитка, керамогранит на клею
- инженерная доска (покрытие пола)
- металлический профиль (порог, Т-профиль, короб двери)
- гидроизоляция (обмазочная, лента)

Примечания

1. Узлы — типовые решения проекта для мест, отмеченных выносками на листе схемы расположения развёрток и узлов; размеры — в мм, отметки — в м от ±0,000 (чистый пол 1-го этажа).
2. Узлы с гидроизоляцией, закладными и коробами скрытого монтажа принимаются по актам скрытых работ до закрытия отделкой; гидроизоляция — после теста проливом (24 ч).
3. Марки изделий (порог, Т-профиль, короб скрытой двери, люк) — по спецификациям; замена — на аналог с теми же габаритами по согласованию с автором проекта.
4. Материал плиты перекрытия и стен в узлах показан условно (железобетон, кладка): конструкция дома не установлена — крепёж, анкеры и толщины слоёв уточняются после обследования (до него — по допущениям общих указаний).
5. Узел 1 применяется на этажах: 1-й этаж, Мансарда; отметки показаны для пом. 8 (1-й этаж), на этаже «Мансарда» — с поправкой +3,150 (разность отметок чистого пола этажей).
6. Узлы комплекта выпущены на 2 листах, нумерация узлов сквозная: 1–4 — лист 205 альбома (данный лист); 5–8 — лист 206 альбома.

Изм.	Кол.уч	Лист	№ док.	Подп.	Дата
Разраб.		Кырлан А.С.			04.11.26
Пров.					
ГИП					
Н. контр.					
Утв.					

ГД-2026-010-АИ

Дом 331 м²

Общая площадь 270,67* м² · * размеры приняты, не замерены (реестр — л. 8–10, К-1)

Дизайн-проект интерьера

Стадия	Лист	Листов
РП	205	216

Узлы. Лист 1 из 2

М 1:5; 1:10

Кырлан Александр Сергеевич


выпуск 04.11.2026 № 2a77323a49 · стр. 209 из 221

Узлы. Лист 2 из 2

Пороги и стыки покрытий, скрытые двери, короба стояков, гидроизоляция, плинтус


5 Гидроизоляция санузла: заход на стены 200 мм, примыкание ванны (М 1:10)

Применение: пом. 3, 15, 20; места — листы 127, 128

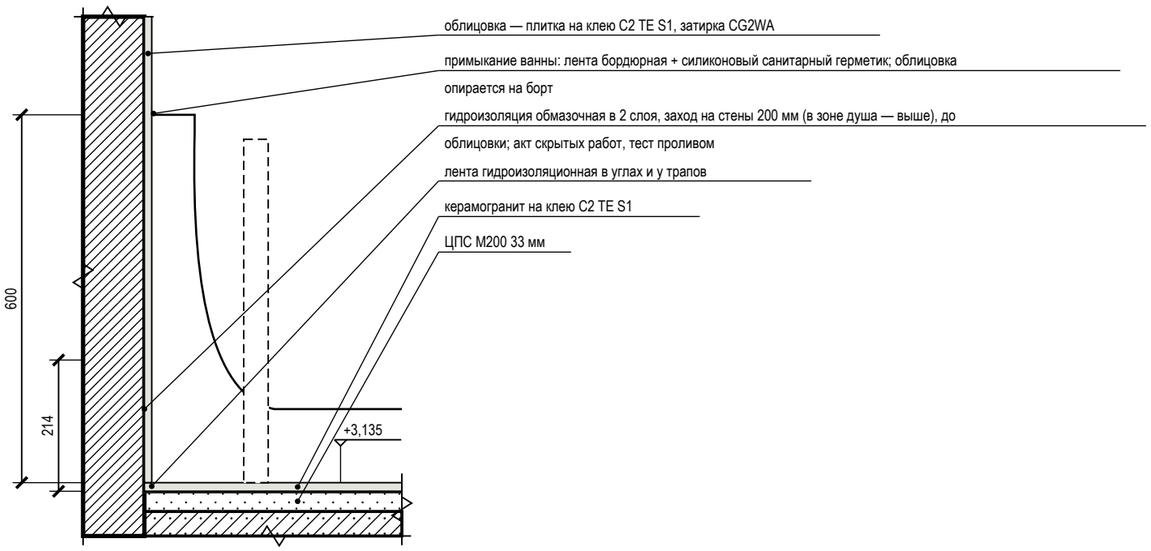

6 Плинтус МДФ 80×16 мм у окрашенной стены по доске (ламинату) (М 1:5)

Применение: пом. 1, 2, 5, 6, 7, 13, 14, 16, 17, 18, 19; места — листы 127, 128

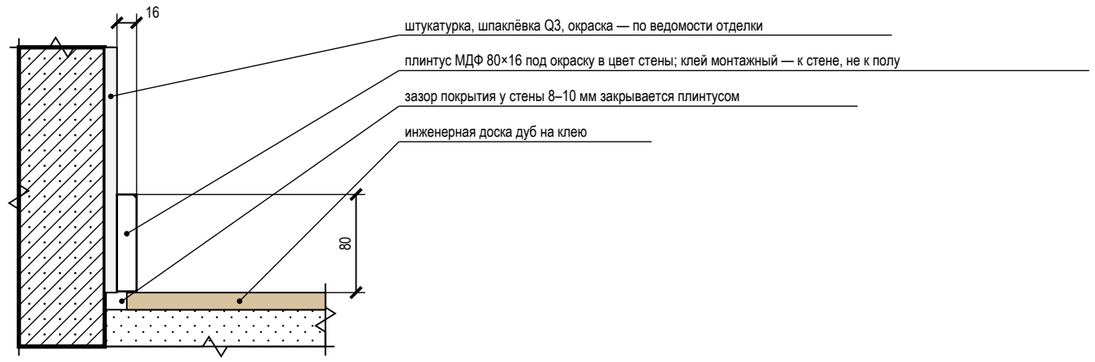


Допущения и предложения на листе

Основа листа: размеры и контуры этажей подобраны проектировщиком по составу помещений и площадям этажей с картинки 470 px (размеры на ней не читаются); обмер и исходный проект — задание (К-1); высоты: 1-й этаж 2800 мм, мансарда 2700 мм (горизонтальная часть) приняты; скаты кровли мансарды приняты по картинке: колено 1200 мм, уклон 45°, конёк вдоль длинной стороны; проект КР — задание (К-2); наружные стены 400 мм, перегородки 120 мм приняты (К-1); разрешённая мощность 15 кВт принята по типовым ТУ для частного дома (К-4); подрайон климата не задан — принят не северный (жилые от 2,5 м) (К-7).

См. лист открытых вопросов (лист 8, записи К-1, К-2, К-4, К-7).


7 Плинтус МДФ 80×16 мм у окрашенной стены по керамограниту (плитке) (М 1:5)

Применение: пом. 4, 8, 9; места — лист 127

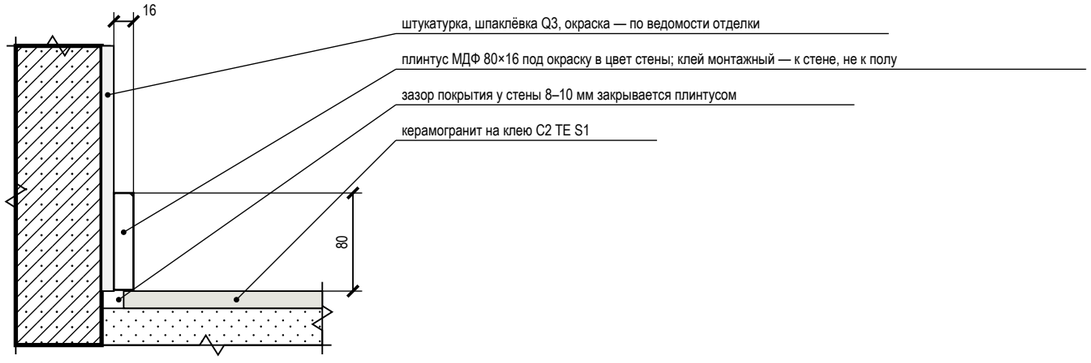

8 Плинтус ПВХ 100×16 мм у окрашенной стены по наливному полу (М 1:5)

Применение: пом. 10; места — лист 127

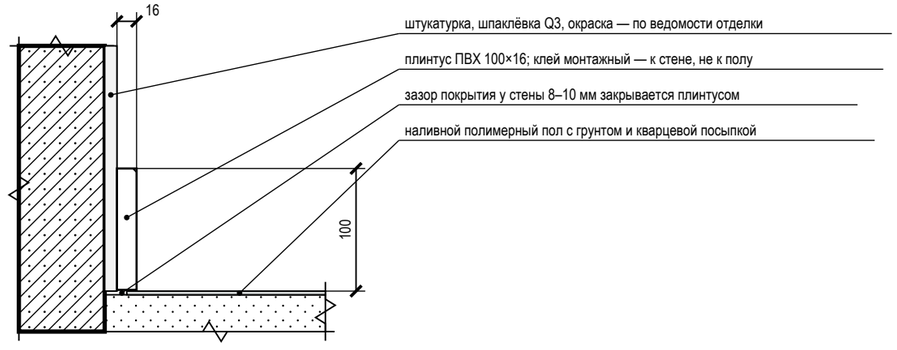

Условные обозначения

- железобетон (плита, стены) — условно: конструкция не установлена
- кладка, перегородка — условно: конструкция не установлена
- стяжка, раствор
- плитка, керамогранит на клею
- инженерная доска (покрытие пола)
- гидроизоляция (обмазочная, лента)

Примечания

1. Узлы — типовые решения проекта для мест, отмеченных выносками на листе схемы расположения развёрток и узлов; размеры — в мм, отметки — в м от ±0,000 (чистый пол 1-го этажа).
2. Узлы с гидроизоляцией, закладными и коробами скрытого монтажа принимаются по актам скрытых работ до закрытия отделкой; гидроизоляция — после теста проливом (24 ч).
3. Марки изделий (порог, Т-профиль, короб скрытой двери, люк) — по спецификациям; замена — на аналог с теми же габаритами по согласованию с автором проекта.
4. Материал плиты перекрытия и стен в узлах показан условно (железобетон, кладка): конструкция дома не установлена — крепёж, анкеры и толщины слоёв уточняются после обследования (до него — по допущениям общих указаний).
5. Узел 5 применяется на этажах: 1-й этаж, Мансарда; отметки показаны для пом. 15 (Мансарда), на этаже «1-й этаж» — с поправкой −3,150 (разность отметок чистого пола этажей).
6. Узлы комплекта выпущены на 2 листах, нумерация узлов сквозная: 1–4 — лист 205 альбома; 5–8 — лист 206 альбома (данный лист).

Изм.	Кол.уч	Лист	№ док.	Подп.	Дата
Разраб.		Кырлан А.С.			04.11.26
Пров.					
ГИП					
Н. контр.					
Утв.					

ГД-2026-010-АИ

Дом 331 м²

Общая площадь 270,67* м² · * размеры приняты, не замерены (реестр — л. 8–10, К-1)

Дизайн-проект интерьера

Стадия	Лист	Листов
РП	206	216

Узлы. Лист 2 из 2

М 1:10; 1:5

Кырлан Александр Сергеевич

выпуск 04.11.2026 № 2a77323a49 · стр. 210 из 221

05

Смета

Кырлан Александр Сергеевич

выпуск 04.11.2026 № 2a77323a49 · стр. 211 из 221

Ведомость объёмов работ

Объёмы по помещениям от чертежа · площади в м², длины в м · формула, правило проёмов и источник в каждой строке

Ведомость объёмов работ по помещениям

Поз.	Наименование работ (материал, число слоёв)	Ед. изм.	Объём по помещениям (№ по экспликации)																				Всего	Формула подсчёта	Правило проёмов	Источник	Цена за ед., ₽	Стоимость, ₽
			1	2	3	4	5	6	7	8	9	10	11	12	13	14	15	16	17	18	19	20						
1. Демонтаж и черновые работы																												
1	Демонтаж существующего покрытия пола до основания	м²	24,59	11,92	4,87	6,88	33,74	10,02	5,99	12,46	3,49	41,58	21,84	3,38	24,59	6,74	6,88	15,52	21,72	17,11	16,28	6,29	295,89	S пом.		л. 19–22	по КП	
2	Демонтаж существующей отделки стен до основания	м²	45,94	30,98	22,48	26,96	45,12	22,29	23,28	38,99	17,07	62,59	49,63	18,73	43,05	25,25	25,50	35,43	40,74	37,80	37,52	24,89	674,24	P × H − проёмы	за вычетом проёмов	л. 19–22	по КП	
3	Демонтаж существующей отделки потолка до основания	м²	24,59	11,92	4,87	6,88	33,74	10,02	5,99	12,46	3,49	41,58	21,84	3,38	24,59	6,74	6,88	15,52	21,72	17,11	16,28	6,29	295,89	S пом.		л. 19–22	по КП	
4	Демонтаж существующих дверных блоков	шт		1	1	1	1		1	1	2	1			1	1	1	1		1	1	1	16	по ведомости проёмов		л. 21–26	по КП	
5	Демонтаж существующих сантехприборов и электрооборудования (если есть)	компл																						по факту на объекте		л. 21, 22	по КП	
6	Устройство стяжки: стяжка ЦПС М300 (В22,5), фибра, по звукоизоляции, 47 мм	м²	24,70	12,06	4,92	7,06	34,04	10,36	6,12	12,68	3,60	42,23			24,68	6,82	6,92	15,62	22,10	17,23	16,33	6,34	273,81	S пом. + S в дверных проёмах (b × t/2)	проёмы добавлены	л. 88, 89, 91–94	530	145 119
7	Гидроизоляция обмазочная, 2 слоя: пол, стены на 200 мм, зоны замачивания	м²			13,78												14,15					12,91	40,84	пол + (P − двери) × h заведения + зоны замачивания		л. 82	450	18 378
8	Штукатурка стен по маякам, до 10 мм	м²	45,94	30,98	22,48	26,96	45,12	22,29	23,28	38,99	17,07	62,59	49,63	18,73	43,05	25,25	25,50	35,43	40,74	37,80	37,52	24,89	674,24	P × H − проёмы по обводу коробок − грани перегородок на ГКЛВ	за вычетом проёмов	л. 19, 20, 91–94	530	357 347
9	Штукатурка оконных откосов шириной более 200 мм	м²	2,97	1,45		0,86	3,04					0,99	5,25		2,90		0,79	1,45		1,45	2,90		24,05	Σ (2h + b) × глубина откоса	откосы > 200 мм	л. 19, 20	540	12 987
10	Потолок ГКЛ по каркасу П113, 1 слой	м²	24,59	11,92	4,87		33,74	6,92		12,46					24,59		6,88	15,52	21,72	17,11	16,28	6,29	202,89	S пом. по плану потолков		л. 73–81	1 500	304 335
11	Балки декоративные 150×120 мм под потолком (фальш-балка, массив лиственницы под маслом): изделие и монтаж на закладные	м					20,76	3,76							7,32				14,40				46,24	4 шт. по плану потолков		л. 73–81	по КП	
Итого по разделу 1 — 838 166 ₽ (позиций 11, из них по КП 6); в сводную смету — л. 215, 216																												
2. Инженерные системы																												
12	Прокладка кабеля ВВГнг(А)-LS по группам щита: за потолком и в штробах стен (штробы — только после технического заключения, см. строку «Штробы в стенах»)	м																					1120,30	Σ длин групп щита		л. 46, 47	60	67 218
13	Прокладка слаботочной линии: Кабель домофона — тип по системе поставщика, отдельно от силовых	м																					2,80	по лучам от ЩС**: 1 точ., запас 10 %		л. 50, 51	по КП	
14	Прокладка слаботочной линии: Кабель коаксиальный RG-6 (75 Ом) к розеткам ТВ, отдельно от силовых	м																					70,60	по лучам от ЩС**: 5 точ., запас 10 %		л. 50, 51	по КП	

Допущения и предложения на листе

Основа листа: размеры и контуры этажей подобраны проектировщиком по составу помещений и площадям этажей с картинки 470 px (размеры на ней не читаются); обмер и исходный проект — задание (К-1); высоты: 1-й этаж 2800 мм, мансарда 2700 мм (горизонтальная часть) приняты; скаты кровли мансарды приняты по картинке: колено 1200 мм, уклон 45°, конёк вдоль длинной стороны; проект КР — задание (К-2); наружные стены 400 мм, перегородки 120 мм приняты (К-1); разрешённая мощность 15 кВт принята по типовым ТУ для частного дома (К-4); подрайон климата не задан — принят не северный (жилые от 2,5 м) (К-7).

Знак «**» — предложение проектировщика, заказчиком не утверждено (согласовать с заказчиком): ЩС — щит слаботочный: место и состав.

См. лист открытых вопросов (лист 8, записи К-1, К-2, К-4, К-7).

Изм.	Кол.уч	Лист	№ док.	Подп.	Дата
Разраб.		Кырлан А.С.			04.11.26
Пров.					
ГИП					
Н. контр.					
Утв.					

ГД-2026-010-АИ

Дом 331 м²

Общая площадь 270,67* м² · * размеры приняты, не замерены (реестр — л. 8–10, К-1)

Дизайн-проект интерьера

Стадия	Лист	Листов
РП	207	216

Ведомость объёмов работ

М б/м

Кырлан Александр Сергеевич

Ведомость объёмов работ (продолжение)

Объёмы по помещениям от чертежа · площади в м², длины в м · формула, правило проёмов и источник в каждой строке

Ведомость объёмов работ по помещениям (продолжение)

Поз.	Наименование работ (материал, число слоёв)	Ед. изм.	Объём по помещениям (№ по экспликации)																				Всего	Формула подсчёта	Правило проёмов	Источник	Цена за ед., ₽	Стоимость, ₽
			1	2	3	4	5	6	7	8	9	10	11	12	13	14	15	16	17	18	19	20						
15	Прокладка слаботочной линии: Кабель U/UTP кат. 5e (LAN, Wi-Fi и камеры по PoE), отдельно от силовых	м																					11,90	по лучам от ЩС**: 1 точ., запас 10 %		л. 50, 51	по КП	
16	Прокладка слаботочной линии: Кабель U/UTP кат. 6 (LAN, Wi-Fi и камеры по PoE), отдельно от силовых	м																					96,40	по лучам от ЩС**: 7 точ., запас 10 %		л. 50, 51	по КП	
17	Прокладка гофротрубы Ø20 для слаботочных линий, отдельно от силовых	м																					163,50	по длине лучей без участков в канале плинтуса (≈ 90 %)		л. 50, 51	по КП	
18	Сборка слаботочного щита ЩС**: корпус, патч-панель, подключение линий и питания 220 В; коммутатор и точки доступа — оборудование заказчика	шт																					1	один щит		л. 43–45, 50, 51	по КП	
19	Электроточка: подрозетник в бетоне, розетка, выключатель, вывод	шт	16	11	4	2	11	4		8	2	5	1	1	10		4	11	5	11	11	3	120	по ведомости электроточек		л. 37, 38, 43–45	950	114 000
20	Штробы в стенах под спуски кабеля к точкам — выполняются только после технического заключения о несущих стенах	м	24,55	21,80	5,36	3,50	20,90	7,80		12,40	3,80	7,60	2,53	2,53	18,00		5,36	19,60	9,10	19,60	19,60	3,80	207,83	Σ (H − h) по точкам на стенах: вертикальные спуски	после техзаключения	л. 21, 22, 37, 38	по КП	
21	Установка встраиваемого точечного светильника	шт	7	6	3		8	2		4					8		3	6	2	6	6	2	63	по плану освещения		л. 39, 40	750	47 250
22	Монтаж светильника: потолочного, подвесного, настенного	шт		2	1	1	1		1		1	2	1	1	2	1	1	2		2	2	1	22	по плану освещения		л. 39, 40	1 200	26 400
23	Монтаж LED-ленты в алюминиевый профиль	м	11,40	5,40			21,10			1,80					6,00			3,20		15,50	6,00		70,40	Σ длин лент по плану освещения		л. 39, 40	230	16 192
24	Установка блока питания LED в доступном месте (люк, шкаф)	шт	2	1			1			1					1			1		1	1		9	один на LED-группу		л. 39, 40	570	5 130
25	Установка автономного пожарного извещателя	шт	1	1			1	1		1	1				1			1	1	1	1		11	по плану розеток		л. 37, 38	по КП	
26	Сборка щита: установка автоматов и АВДТ групп, вводного автомата	шт																					22	группы + вводной автомат		л. 46, 47	230	5 060
27	Установка вводного УЗО	шт																					1	по однолинейной схеме		л. 46, 47	380	380
28	Монтаж инсталляции, установка подвесного унитаза и кнопки смыва	шт			1												1					1	3	по плану выводов		л. 56, 57, 70	10 500	31 500
29	Короб инсталляции: каркас и обшивка ГКЛВ в 2 слоя, ревизионный доступ к смыву	шт			1												1					1	3	по плану выводов		л. 56, 57, 82–87	по КП	
30	Короб К1 над чистым полом: каркас и обшивка ГКЛВ под плитку (материалы в спецификации ВК)	м.п.	1,28		3,21												2,88					5,83	13,20	Σ открытых участков выпусков К1 (профиль листа разводки ВК)		л. 56, 57, 70	по КП	
31	Установка ванны с сифоном	шт															1						1	по плану выводов		л. 56, 57, 70	6 000	6 000

Допущения и предложения на листе

Основа листа: размеры и контуры этажей подобраны проектировщиком по составу помещений и площадям этажей с картинки 470 px (размеры на ней не читаются); обмер и исходный проект — задание (К-1); высоты: 1-й этаж 2800 мм, мансарда 2700 мм (горизонтальная часть) приняты; скаты кровли мансарды приняты по картинке: колено 1200 мм, уклон 45°, конёк вдоль длинной стороны; проект КР — задание (К-2); наружные стены 400 мм, перегородки 120 мм приняты (К-1); разрешённая мощность 15 кВт принята по типовым ТУ для частного дома (К-4); подрайон климата не задан — принят не северный (жилые от 2,5 м) (К-7).

Знак «**» — предложение проектировщика, заказчиком не утверждено (согласовать с заказчиком): ЩС — щит слаботочный: место и состав.

См. лист открытых вопросов (лист 8, записи К-1, К-2, К-4, К-7).

Изм.	Кол.уч	Лист	№ док.	Подп.	Дата
Разраб.		Кырлан А.С.			04.11.26
Пров.					
ГИП					
Н. контр.					
Утв.					

ГД-2026-010-АИ

Дом 331 м²

Общая площадь 270,67* м² · * размеры приняты, не замерены (реестр — л. 8–10, К-1)

Дизайн-проект интерьера

Стадия	Лист	Листов
РП	208	216

Ведомость объёмов работ (продолжение)

М б/м

Кырлан Александр Сергеевич

Ведомость объёмов работ (продолжение)

Объёмы по помещениям от чертежа · площади в м², длины в м · формула, правило проёмов и источник в каждой строке

Ведомость объёмов работ по помещениям (продолжение)

Поз.	Наименование работ (материал, число слоёв)	Ед. изм.	Объём по помещениям (№ по экспликации)																			Всего	Формула подсчёта	Правило проёмов	Источник	Цена за ед., ₽	Стоимость, ₽
			1	2	3	4	5	6	7	8	9	10	11	12	13	14	15	16	17	18	19	20						
32	Установка умывальника (мойки) с сифоном и смесителем	шт			1												1					1	3	по плану выводов		л. 56, 57, 70	3 000	9 000
33	Установка душевого поддона с трапом, ограждения	шт			1																	1	2	по плану выводов		л. 56, 57, 70	по КП	
34	Подключение стиральной (посудомоечной) машины к ВК	шт																				1	1	по плану выводов		л. 56, 57	по КП	
35	Установка радиатора с узлом подключения и терморегулятором	шт	2	1			2								2			1		1	2		11	по плану отопления		л. 54, 55	по КП	
Итого по разделу 2 — 328 130 ₽ (позиций 24, из них по КП 13); в сводную смету — л. 215, 216																											
3. Чистовые работы																											
36	Облицовка стен керамогранитом 600×1200 на клею	м²			19,67												19,01					17,04	55,72	по раскладке: зона облицовки − место за коробом	за вычетом проёмов	л. 82–87	2 500	139 300
37	Облицовка короба инсталляции (ГКЛВ) керамогранитом: лицо, боковины, полка	м²			1,64												1,73					1,47	4,84	по раскладке: лицо, боковины, полка		л. 82–87	2 500	12 100
38	Укладка керамогранита на пол, 600×600, на клею	м²			4,92	7,06				12,68	3,60		21,98	3,44			6,92					6,34	66,94	S пом. + S в дверных проёмах	проёмы добавлены	л. 82–89	1 800	120 492
39	Затирка швов керамогранита	м²			26,18	6,88				12,46	3,49		21,84	3,38			27,62					24,80	126,65	Σ S облицовки и пола из плитки		л. 82–87	150	18 998
40	Грунтование стен, 2 слоя (под штукатурку и под отделку)	м²	45,94	30,98	22,48	26,96	45,12	22,29	23,28	38,99	17,07	62,59	49,63	18,73	43,05	25,25	25,50	35,43	40,74	37,80	37,52	24,89	674,24	P × H − проёмы	за вычетом проёмов	л. 91–94	96	64 727
41	Шпаклёвка стен под окраску, 2 слоя (старт и финиш), уровень К3	м²	45,94	30,98		26,96	45,12	22,29	23,28	38,99	17,07	62,59	49,63	18,73	43,05	25,25		35,43	40,74	37,80	37,52		601,37	P × H − проёмы − фартук	за вычетом проёмов	л. 91–94	750	451 028
42	Грунтование и шпаклёвка оконных откосов, 2 слоя	м.п.	9,00	4,40		2,60	9,20					3,00	15,90		8,80			4,40		4,40	8,80		70,50	Σ (2h + b) по окнам	по окнам	л. 19, 20	300	21 150
43	Грунтование потолка, 2 слоя	м²	24,59	11,92	4,87	6,88	33,74	10,02	5,99	12,46	3,49	41,58	21,84	3,38	24,59	6,74	6,88	15,52	21,72	17,11	16,28	6,29	295,89	S пом.		л. 91–94	96	28 405
44	Шпаклёвка потолка под окраску, 2 слоя, уровень Q3	м²	24,59	11,92	4,87	6,88	33,74	10,02	5,99	12,46	3,49	41,58	21,84	3,38	24,59	6,74	6,88	15,52	21,72	17,11	16,28	6,29	295,89	S пом.		л. 73–81, 91–94	950	281 096
45	Окраска потолка водно-дисперсионной краской, 2 слоя	м²	24,59	11,92	4,87	6,88	33,74	10,02	5,99	12,46	3,49	41,58	21,84	3,38	24,59	6,74	6,88	15,52	21,72	17,11	16,28	6,29	295,89	S пом.		л. 91–94	360	106 520
46	Окраска стен водно-дисперсионной краской, 2 слоя	м²	54,43	37,91		29,57	60,42	34,34	27,78	46,55	21,06	72,46	64,75	20,83	50,40	28,19		41,10	54,18	44,10	43,40		731,47	P × H − фартук, проёмы не вычитаются	без вычета проёмов	л. 91–94	300	219 441
47	Окраска оконных откосов, 2 слоя	м.п.	9,00	4,40		2,60	9,20					3,00	15,90		8,80			4,40		4,40	8,80		70,50	Σ (2h + b) по окнам	по окнам	л. 19, 20	120	8 460
48	Укладка инженерной доски на клей	м²	24,70	12,06			34,04	10,36	6,12						24,68	6,82		15,62	22,10	17,23	16,33		190,06	S пом. + S в дверных проёмах	проёмы добавлены	л. 88, 89, 91–94	1 200	228 072
49	Установка плинтуса МДФ h=80 мм	м.п.	18,26	11,74		9,66	18,24	6,98	7,78	13,64	5,62				18,66	9,04		14,74	14,44	15,64	16,56		181,00	P − ширина дверных проёмов		л. 91–94	450	81 450
50	Установка плинтуса ПВХ h=100 мм	м.п.										21,98											21,98	P − ширина дверных проёмов		л. 91–94	450	9 891

Допущения и предложения на листе

Основа листа: размеры и контуры этажей подобраны проектировщиком по составу помещений и площадям этажей с картинки 470 px (размеры на ней не читаются); обмер и исходный проект — задание (К-1); высоты: 1-й этаж 2800 мм, мансарда 2700 мм (горизонтальная часть) приняты; скаты кровли мансарды приняты по картинке: колено 1200 мм, уклон 45°, конёк вдоль длинной стороны; проект КР — задание (К-2); наружные стены 400 мм, перегородки 120 мм приняты (К-1); разрешённая мощность 15 кВт принята по типовым ТУ для частного дома (К-4); подрайон климата не задан — принят не северный (жилые от 2,5 м) (К-7).

См. лист открытых вопросов (лист 8, записи К-1, К-2, К-4, К-7).

Изм.	Кол.уч	Лист	№ док.	Подп.	Дата
Разраб.		Кырлан А.С.			04.11.26
Пров.					
ГИП					
Н. контр.					
Утв.					

ГД-2026-010-АИ

Дом 331 м²

Общая площадь 270,67* м² · * размеры приняты, не замерены (реестр — л. 8–10, К-1)

Дизайн-проект интерьера

Стадия	Лист	Листов
РП	209	216

Ведомость объёмов работ (продолжение)

М б/м

Кырлан Александр Сергеевич

Ведомость объёмов работ (продолжение)

Объёмы по помещениям от чертежа · площади в м², длины в м · формула, правило проёмов и источник в каждой строке

Ведомость объёмов работ по помещениям (продолжение)

Поз.	Наименование работ (материал, число слоёв)	Ед. изм.	Объём по помещениям (№ по экспликации)																				Всего	Формула подсчёта	Правило проёмов	Источник	Цена за ед., ₽	Стоимость, ₽
			1	2	3	4	5	6	7	8	9	10	11	12	13	14	15	16	17	18	19	20						
51	Плинтус из керамогранита: нарезка полос из плитки пола, запил кромки 45°, установка h=80 мм	м.п.											20,48	6,36									26,84	P − ширина дверных проёмов		л. 91–94	930	24 961
52	Окраска плинтуса в тоне S 0804-Y30R, 2 слоя	м.п.	18,26	11,74		9,66	18,24	6,98	7,78	13,64	5,62				18,66	9,04		14,74	14,44	15,64	16,56		181,00	как плинтус		л. 91–94	300	54 300
53	Монтаж дверей скрытого монтажа под покраску (поставщик дверей)	шт		1	1										1	1	1	1		1	1	1	9	по ведомости проёмов		л. 23–26	5 250	47 250
54	Монтаж межкомнатных дверей (поставщик дверей)	шт					1		1	1	1												4	по ведомости проёмов		л. 23–26	5 250	21 000
55	Входная дверь, поставка с монтажом и откосами	шт																					3	по ведомости проёмов		л. 23–26	по КП	
Итого по разделу 3 — 1 938 641 ₽ (позиций 20, из них по КП 1); в сводную смету — л. 215, 216																												

Допущения и предложения на листе

Основа листа: размеры и контуры этажей подобраны проектировщиком по составу помещений и площадям этажей с картинки 470 px (размеры на ней не читаются); обмер и исходный проект — задание (К-1); высоты: 1-й этаж 2800 мм, мансарда 2700 мм (горизонтальная часть) приняты; скаты кровли мансарды приняты по картинке: колено 1200 мм, уклон 45°, конёк вдоль длинной стороны; проект КР — задание (К-2); наружные стены 400 мм, перегородки 120 мм приняты (К-1); разрешённая мощность 15 кВт принята по типовым ТУ для частного дома (К-4); подрайон климата не задан — принят не северный (жилые от 2,5 м) (К-7).

См. лист открытых вопросов (лист 8, записи К-1, К-2, К-4, К-7).

Изм.	Кол.уч	Лист	№ док.	Подп.	Дата
Разраб.		Кырлан А.С.			04.11.26
Пров.					
ГИП					
Н. контр.					
Утв.					

ГД-2026-010-АИ

Дом 331 м²

Общая площадь 270,67* м² · * размеры приняты, не замерены (реестр — л. 8–10, К-1)

Дизайн-проект интерьера

Стадия	Лист	Листов
РП	210	216

Ведомость объёмов работ (продолжение)

М б/м

Кырлан Александр Сергеевич

Ведомость объёмов работ (окончание)

Объёмы по помещениям от чертежа · площади в м², длины в м · формула, правило проёмов и источник в каждой строке

Ведомость подсчёта площадей по помещениям

№	Помещение	S пола, м²	P, м	H, м	P × H, м²	Проёмы, м²	Стены нетто, м²	В дверных проёмах, м²	Плинтус, м	Откосы, м.п.
1	Кухня-столовая	24,59	20,16	2,70	54,43	8,49	45,94	0,11	18,26	9,00
2	Кабинет-гостевая	11,92	14,04	2,70	37,91	6,93	30,98	0,14	11,74	4,40
3	Санузел 1 этажа	4,87	9,24	2,62	24,16	1,68	22,48	0,05	нет	нет
4	Котельная	6,88	10,56	2,80	29,57	2,61	26,96	0,18	9,66	2,60
5	Гостиная	33,74	23,24	2,60	60,42	15,30	45,12	0,30	18,24	9,20
6	Холл с лестницей	10,02	12,72	2,70	34,34	12,05	22,29	0,34	6,98	нет
7	Кладовая	5,99	9,92	2,80	27,78	4,49	23,28	0,13	7,78	нет
8	Прихожая	12,46	17,24	2,70	46,55	7,56	38,99	0,22	13,64	нет
9	Тамбур	3,49	7,52	2,80	21,06	3,99	17,07	0,11	5,62	нет
10	Гараж	41,58	25,88	2,80	72,46	9,87	62,59	0,65	21,98	3,00
11	Веранда	21,84	22,88	2,83	64,75	15,12	49,63	0,14	20,48	15,90
12	Крыльцо	3,38	7,36	2,83	20,83	2,10	18,73	0,06	6,36	нет
13	Спальня мастер	24,59	20,16	2,50	50,40	7,35	43,05	0,09	18,66	8,80
14	Гардеробная мастер	6,74	10,44	2,70	28,19	2,94	25,25	0,08	9,04	нет
15	Санузел мастер	6,88	10,56	2,62	27,61	2,11	25,50	0,04	нет	2,40
16	Спальня 2	15,52	16,44	2,50	41,10	5,67	35,43	0,10	14,74	4,40
17	Холл мансарды	21,72	20,84	2,60	54,18	13,44	40,74	0,38	14,44	нет
18	Спальня 3	17,11	17,64	2,50	44,10	6,30	37,80	0,12	15,64	4,40
19	Спальня 4	16,28	17,36	2,50	43,40	5,88	37,52	0,05	16,56	8,80
20	Санузел 2	6,29	10,16	2,62	26,57	1,68	24,89	0,05	нет	нет
	Итого	**295,89**			**809,82**	**135,57**	**674,25**	**3,36**	**229,82**	**72,90**

Реестр контрольных сумм

Показатель	По ВОР	По чертежу	Расхождение	Лист
Σ площадей помещений без летних, м² — общая площадь по экспликации	270,67	270,67	0,0 %	л. 19, 20
Стены под окраску, м² (шпаклёвка) ведомость отделки	601,37	575,14	4,6 %	л. 91–94
Потолки под окраску, м² — ведомость отделки	295,89	295,89	0,0 %	л. 91–94
Плинтус, м — ведомость отделки	229,82	229,82	0,0 %	л. 91–94
Плитка к заказу, шт — ведомость плитки	289	289	0,0 %	л. 82
Гидроизоляция, м² — ведомость материалов плитки	40,84	40,83	0,0 %	л. 82
Точки ЭОМ, шт — планы ЭОМ (без щитов)	235	238	-1,3 %	л. 37–40

Примечания

1. Объёмы — от геометрии проекта (та же, что на планах и в ведомости отделки), не от общей площади: P — периметр чистого контура, H — от чистого пола до низа потолка, проёмы — по наружному обводу коробок.
2. Подсчёт по ГЭСН-2001-15 и ГЭСН-2001-11: штукатурка и шпаклёвка стен — за вычетом проёмов; окраска водными составами — без вычета проёмов (п. 2.24); откосы — отдельно, по ширине до 200 и более 200 мм; полы — с площадью в дверных проёмах.
3. Плитка — по раскладке (целые и с подрезкой); короб инсталляции и фартук — отдельными строками, двойного счёта облицовки нет. Материалы, запас и количество к заказу — в спецификации материалов.
4. Цены — ориентир по открытым прайсам Москвы (прайсы собраны 21.09.2026, часть расценок сверена повторно 24.09.2026), не коммерческое предложение; «по КП» — расценки нет, строка в итог не входит.
5. Демонтаж — по плану демонтажа и общим указаниям: покрытия пола, отделка стен и потолков, дверные блоки — до основания; объёмы справочные — по плану демонтажа (расценки в книге нет — «по КП»).
6. Штробы в стенах — только после технического заключения о несущих стенах (общие указания, план обмера и демонтажа): строка «Штробы в стенах» вертикальные спуски кабеля от потолочной трассы к точкам, объём не меньше фактического (горизонтальные трассы — по исполнительной схеме). Расценки штробления в прайсе нет — «по КП», в итог не входит; кабель в штробах стен прокладывается после неё.
7. Площадь облицовки стен — одно число с тремя названиями: зона облицовки по ведомости отделки 58,23 м² − место за коробом инсталляции 2,51 м² (плитку туда не кладут) = стены под плитку 55,72 м² (строка «Облицовка стен»); облицовка коробов 4,84 м² — отдельной строкой; стены и короба вместе — 60,56 м² (столько плитки по раскладке в спецификации). Источник — один (quantities.js), расхождение на листах ловит.
8. Слаботочные сети: кабель по лучам от ЩС** 181,70 м (U/UTP, RG-6, домофон — по видам), гофра 163,50 м, щит ЩС** с патч-панелью; розетки RJ45 и ТВ монтируются в строке «Электроточка». Длины те же, что в ведомости изделий электрика (одна модель — lowcurrent-engineer/bom.js); оборудование заказчика (точки доступа, камеры, коммутатор) в спецификацию не входит. 2 точ. — предложение листа слаботочки.
9. Коробы: стояков (нет) и К1 над чистым полом (13,20 м открытых участков; труба К1 вдоль стен 32,44 м в короб не зашивается — она за приборами, в раме инсталляции и в шахтах). В спецификации ВК короб К1 заказывается с запасом 10 % — 14,60 м. Материалы коробов стояков и инсталляции — в спецификации материалов, К1 — в спецификации ВК.

Допущения и предложения на листе

Основа листа: размеры и контуры этажей подобраны проектировщиком по составу помещений и площадям этажей с картинки 470 px (размеры на ней не читаются); обмер и исходный проект — задание (К-1); высоты: 1-й этаж 2800 мм, мансарда 2700 мм (горизонтальная часть) приняты; скаты кровли мансарды приняты по картинке: колено 1200 мм, уклон 45°, конёк вдоль длинной стороны; проект КР — задание (К-2); наружные стены 400 мм, перегородки 120 мм приняты (К-1); разрешённая мощность 15 кВт принята по типовым ТУ для частного дома (К-4); подрайон климата не задан — принят не северный (жилые от 2,5 м) (К-7).

Знак «**» — предложение проектировщика, заказчиком не утверждено (согласовать с заказчиком): ЩС — щит слаботочный: место и состав.

См. лист открытых вопросов (лист 8, записи К-1, К-2, К-4, К-7).

Изм.	Кол.уч	Лист	№ док.	Подп.	Дата
Разраб.		Кырлан А.С.			04.11.26
Пров.					
ГИП					
Н. контр.					
Утв.					

ГД-2026-010-АИ

Дом 331 м²

Общая площадь 270,67* м² · * размеры приняты, не замерены (реестр — л. 8–10, К-1)

Дизайн-проект интерьера

Стадия	Лист	Листов
РП	211	216

Ведомость объёмов работ (окончание)

М б/м

Кырлан Александр Сергеевич

выпуск 04.11.2026 № 2a77323a49 · стр. 216 из 221

Спецификация материалов

Отделочные материалы: чистое количество, запас, упаковка, к заказу · ГОСТ 21.110-2013

Спецификация материалов (ГОСТ 21.110-2013, форма 1)

Поз.	Наименование и техническая характеристика	Тип, марка, артикул	Код продукции	Поставщик	Ед. изм.	Количество				Масса ед., кг	Примечание
						чистое	запас, %	упаковка	к заказу		
Покрытия полов и облицовка											
1	Инженерная доска (дуб натуральный, рабочий слой 4 мм, эмиссия E1, прямая укладка)	1167-4250			м²	190,07	7	по артикулу	203,40 м²		пом. 1, 2, 5, 6, 7, 13, 14, 16, 17, 18, 19; до целой упаковки; л. 88, 89, 91–94
2	Клей для паркетной и инженерной доски (эластичный, по ТУ изготовителя доски)	по выбору подрядчика			м²	190,07		ведро по ТУ	по ТУ		расход кг/м² — по ТУ клея; л. 88, 89
3	Керамогранит 600×600 мм под травертин	аналог: керамогранит под травертин			шт	56	10	коробка	62 шт		14 целых + 42 с подрезкой; 18,04 м² по раскладке, к заказу 22,32 м²; пом. 3, 15, 20; л. 82–87
4	Керамогранит 600×1200 мм A8UZ	A8UZ			шт	202	10	коробка	227 шт		56 целых + 146 с подрезкой; 108,61 м² по раскладке, к заказу 163,44 м²; пом. 3, 4, 8, 9, 11, 12, 15, 20; л. 82–87
Сухие смеси и гидроизоляция											
5	Клей плиточный цементный класса C2 TE S1 (ГОСТ Р 56387-2018)	Ceresit CM 17 или аналог			кг	981,02	10	мешок 25 кг	44 меш.	25	слой 5 мм, 1,50 кг/м² на 1 мм; л. 82
6	Затирка цементная класса CG2WA, цвет — по колерной карте	Mapei Ultracolor Plus 132 или аналог			кг	10,01	10	упак. 2 кг	6 упак.	2	расход (a+b)/ab × шов × t × 1,6 кг/м²; л. 82
7	Гидроизоляция обмазочная полимерная, 2 слоя, лента в углах, манжеты на выводах	по выбору подрядчика			м²	40,84	10	ведро по ТУ	по ТУ		пом. 3, 15, 20; расход кг/м² — по ТУ; л. 82
8	Лента демпферная по периметру пола из плитки	по выбору подрядчика			м	82,24	10	рулон	91,00 м		л. 82
9	Смесь цементно-песчаная для стяжки М200 (47 мм, 50 мм, 33 мм, 49 мм, 61 мм)	по выбору подрядчика			м³	13,74	5	мешок по ТУ	по ТУ		S 273,81 м² × толщина; армирование и маяки — по ТУ; л. 88, 89
10	Смесь штукатурная гипсовая для машинного и ручного нанесения по маякам, слой до 10 мм	по выбору подрядчика			м²	674,24	10	мешок по ТУ	по ТУ		пом. 1, 2, 3, 4, 5, 6, 7, 8, 9, 10, 11, 12, 13, 14, 15, 16, 17, 18, 19, 20; расход кг/м² на 1 мм слоя — по ТУ смеси, толщина — по замеру кривизны стен; л. 19, 20, 91–94
Короба из ГКЛВ											
11	Лист ГКЛВ 12,5 мм, 2500 × 1200 мм, обшивка коробов в 2 слоя	по выбору подрядчика			м²	9,68	10	лист 3,00 м²	4,00 лист		инсталляция пом. 3: 1,64 м²; инсталляция пом. 15: 1,73 м²; инсталляция пом. 20: 1,47 м²; площадь × 2 слоя; короб К1 над полом — в спецификации ВК; л. 56, 57, 82–87
12	Профиль стальной оцинкованный 27 × 28 мм: каркас коробов (стойки и направляющие)	по выбору подрядчика			м	23,98	10	хлыст 3 м	9 шт		стойки через 400 мм по свободному периметру + направляющие по полу и потолку; крепёж, лента, шпаклёвка швов — по узлу короба; л. 56, 57, 82–87
Слаботочные сети											
13	Кабель домофона — тип по системе поставщика	по выбору подрядчика			м	2,80		бухта по ТУ	3,00 м		по лучам от ЩС**, 1 точ., запас 10 % уже в длине; 2 точ. — предложение листа слаботочки (знак «*» на плане); л. 50, 51
14	Кабель коаксиальный RG-6 (75 Ом) к розеткам ТВ	по выбору подрядчика			м	70,60		бухта по ТУ	71,00 м		по лучам от ЩС**, 5 точ., запас 10 % уже в длине; 2 точ. — предложение листа слаботочки (знак «*» на плане); л. 50, 51
15	Кабель U/UTP кат. 5e (LAN, Wi-Fi и камеры по PoE)	по выбору подрядчика			м	11,90		бухта по ТУ	12,00 м		по лучам от ЩС**, 1 точ., запас 10 % уже в длине; 2 точ. — предложение листа слаботочки (знак «*» на плане); л. 50, 51

Допущения и предложения на листе

Основа листа: размеры и контуры этажей подобраны проектировщиком по составу помещений и площадям этажей с картинки 470 px (размеры на ней не читаются); обмер и исходный проект — задание (К-1); высоты: 1-й этаж 2800 мм, мансарда 2700 мм (горизонтальная часть) приняты; скаты кровли мансарды приняты по картинке: колено 1200 мм, уклон 45°, конёк вдоль длинной стороны; проект КР — задание (К-2); наружные стены 400 мм, перегородки 120 мм приняты (К-1); разрешённая мощность 15 кВт принята по типовым ТУ для частного дома (К-4); подрайон климата не задан — принят не северный (жилые от 2,5 м) (К-7).

Знак «*» — принято, не замерено и не подтверждено (замерить на объекте): К-13: пол пом. 11, 12 — отметка верха плиты −0,170 принята по пирогу (плита веранды и крыльца своя, ниже плиты дома) — подтвердить по проекту КР или обмером (К-13).

Знак «**» — предложение проектировщика, заказчиком не утверждено (согласовать с заказчиком): ЩС — щит слаботочный: место и состав; плинтус пом. 1, 2, 4–14, 16, 17, фартук пом. 1, акцент пом. 5 — артикул изделия не выбран: позиция описана характеристиками («аналог по характеристикам»), артикул выбирается при закупке; пол пом. 3, 15, 20 — пирог пола: стяжка 33 мм и обмазочная гидроизоляция добавлены разработчиком проекта; артикул изделия не выбран: позиция описана характеристиками («аналог по характеристикам»), артикул выбирается при закупке; пол пом. 10 — покрытие пола гаража — предложение исполнителя: выдерживает шины, масло и антигололёдные реагенты, без швов.

См. лист открытых вопросов (лист 8, записи К-1, К-2, К-4, К-7; лист 9, запись К-13).

Изм.	Кол.уч	Лист	№ док.	Подп.	Дата
Разраб.		Кырлан А.С.			04.11.26
Пров.					
ГИП					
Н. контр.					
Утв.					

ГД-2026-010-АИ

Дом 331 м²

Общая площадь 270,67* м² · * размеры приняты, не замерены (реестр — л. 8–10, К-1)

Дизайн-проект интерьера

Стадия	Лист	Листов
РП	212	216

Спецификация материалов

М б/м

Кырлан Александр Сергеевич

Спецификация материалов (продолжение)

Отделочные материалы: чистое количество, запас, упаковка, к заказу · ГОСТ 21.110-2013

Спецификация материалов (ГОСТ 21.110-2013, форма 1) (продолжение)

Поз.	Наименование и техническая характеристика	Тип, марка, артикул	Код продукции	Поставщик	Ед. изм.	Количество				Масса ед., кг	Примечание
						чистое	запас, %	упаковка	к заказу		
16	Кабель U/UTP кат. 6 (LAN, Wi-Fi и камеры по PoE)	по выбору подрядчика			м	96,40		бухта по ТУ	97,00 м		по лучам от ЩС**, 7 точ., запас 10 % уже в длине; 2 точ. — предложение листа слаботочки (знак «*» на плане); л. 50, 51
17	Гофротруба Ø20 для слаботочных линий, отдельно от силовых	по выбору подрядчика			м	163,50		бухта по ТУ	164,00 м		по длине лучей без участков в канале плинтуса (≈ 90 %); л. 50, 51
18	Розетка компьютерная RJ45, кат. 6, с рамкой и подрозетником	по выбору подрядчика			шт	7		шт	7 шт		LAN1–LAN6, LAN7**; серия механизмов — как у розеток и выключателей; л. 43–45, 50, 51
19	Розетка телевизионная (коаксиальная) с рамкой и подрозетником	по выбору подрядчика			шт	5		шт	5 шт		ТВ1–ТВ5; серия механизмов — как у розеток и выключателей; л. 43–45, 50, 51
20	Трубка или монитор домофона (поставка домофонной организации)	по выбору подрядчика			шт	1		шт	1 шт		ДФ1; серия механизмов — как у розеток и выключателей; л. 43–45, 50, 51
21	Щит слаботочный ЩС**: корпус, DIN-рейка, розетки 220 В	по выбору подрядчика			шт	1		шт	1 шт		ЩС**; серия механизмов — как у розеток и выключателей; л. 43–45, 50, 51
22	Патч-панель, портов не менее 8	по выбору подрядчика			шт	1		шт	1 шт		серия механизмов — как у розеток и выключателей; л. 43–45, 50, 51
Лакокрасочные материалы											
23	Краска интерьерная акриловая, полуматовая, класс истирания 1	Tikkurila Luja 7 S 0804-Y30R «S 0804-Y30R»			л	27,43	10	банка 2,7 л	12 банк		114,30 м² × 2 сл. × 0,12 л/м²; пом. 1, 11, 12; л. 91–94
24	Краска интерьерная акриловая, матовая, класс истирания 1	Tikkurila Luja 7 S 0804-Y30R «S 0804-Y30R»			л	11,95	10	банка 2,7 л	5 банк		49,81 м² × 2 сл. × 0,12 л/м²; пом. 1 (пот.), 11 (пот.), 12 (пот.); л. 91–94
25	Краска интерьерная акриловая, матовая, класс истирания 1	Farrow & Ball Modern Emulsion No. 298 «Bancha»			л	1,36	10	банка 2,5 л	1 банк		5,68 м² × 2 сл. × 0,12 л/м²; пом. 2; л. 91–94
26	Краска интерьерная акриловая, матовая, класс истирания 1	Farrow & Ball Modern Emulsion No. 226 «Joa's White»			л	78,23	10	банка 2,5 л	35 банк		325,94 м² × 2 сл. × 0,12 л/м²; пом. 2, 4, 6, 8, 9, 10, 13, 16, 17, 18, 19; л. 91–94
27	Краска интерьерная акриловая, глубокоматовая, класс истирания 2	Little Greene Absolute Matt No. 105 «Slaked Lime»			л	46,63	10	фасовка по артикулу	51,30 л		194,30 м² × 2 сл. × 0,12 л/м²; пом. 2 (пот.), 4 (пот.), 6 (пот.), 7 (пот.), 8 (пот.), 9 (пот.), 10 (пот.), 13 (пот.), 14 (пот.), 16 (пот.), 17 (пот.), 18 (пот.), 19 (пот.); л. 91–94
28	Краска интерьерная акриловая, матовая, класс истирания 1	Little Greene Intelligent Bathroom No. 105 «Slaked Lime»			л	4,33	10	фасовка по артикулу	4,80 л		18,04 м² × 2 сл. × 0,12 л/м²; пом. 3 (пот.), 15 (пот.), 20 (пот.); л. 91–94
29	Краска интерьерная акриловая, матовая, класс истирания 1	Farrow & Ball Modern Emulsion No. 93 «Studio Green — почти чёрный зелёный»			л	4,65	10	банка 2,5 л	3 банк		12,92 м² × 3 сл. × 0,12 л/м²; пом. 5; л. 91–94
30	Краска интерьерная акриловая, матовая, класс истирания 2	Tikkurila Optiva 5 Matt S 0804-Y30R «S 0804-Y30R»			л	7,73	10	банка 2,7 л	4 банк		32,20 м² × 2 сл. × 0,12 л/м²; пом. 5; л. 91–94
31	Краска интерьерная акриловая, глубокоматовая, класс истирания 2	Tikkurila Anti-Reflex 2 S 0804-Y30R «S 0804-Y30R»			л	8,10	10	банка 2,7 л	4 банк		33,74 м² × 2 сл. × 0,12 л/м²; пом. 5 (пот.); л. 91–94
32	Краска интерьерная акриловая, матовая, класс истирания 1	Little Greene Intelligent Matt No. 105 «Slaked Lime»			л	10,07	10	фасовка по артикулу	11,10 л		41,96 м² × 2 сл. × 0,12 л/м²; пом. 7, 14; л. 91–94
33	Краска интерьерная акриловая, матовая, класс истирания 2	Tikkurila Optiva 5 Matt S 7020-G10Y «Хвойный тёмно-зелёный»			л	1,82	10	банка 2,7 л	1 банк		7,60 м² × 2 сл. × 0,12 л/м²; пом. 13; л. 91–94

Допущения и предложения на листе

Основа листа: размеры и контуры этажей подобраны проектировщиком по составу помещений и площадям этажей с картинки 470 px (размеры на ней не читаются); обмер и исходный проект — задание (К-1); высоты: 1-й этаж 2800 мм, мансарда 2700 мм (горизонтальная часть) приняты; скаты кровли мансарды приняты по картинке: колено 1200 мм, уклон 45°, конёк вдоль длинной стороны; проект КР — задание (К-2); наружные стены 400 мм, перегородки 120 мм приняты (К-1); разрешённая мощность 15 кВт принята по типовым ТУ для частного дома (К-4); подрайон климата не задан — принят не северный (жилые от 2,5 м) (К-7).

Знак «*» — принято, не замерено и не подтверждено (замерить на объекте): К-13: пол пом. 11, 12 — отметка верха плиты −0,170 принята по пирогу (плита веранды и крыльца своя, ниже плиты дома) — подтвердить по проекту КР или обмером (К-13).

Знак «**» — предложение проектировщика, заказчиком не утверждено (согласовать с заказчиком): ЩС — щит слаботочный: место и состав; LAN7 — розетка LAN у рабочего стола; плинтус пом. 1, 2, 4–14, 16, 17, фартук пом. 1, акцент пом. 5 — артикул изделия не выбран: позиция описана характеристиками («аналог по характеристикам»), артикул выбирается при закупке; пол пом. 3, 15, 20 — пирог пола: стяжка 33 мм и обмазочная гидроизоляция добавлены разработчиком проекта; артикул изделия не выбран: позиция описана характеристиками («аналог по характеристикам»), артикул выбирается при закупке; пол пом. 10 — покрытие пола гаража — предложение исполнителя: выдерживает шины, масло и антигололёдные реагенты, без швов.

См. лист открытых вопросов (лист 8, записи К-1, К-2, К-4, К-7; лист 9, запись К-13).

Изм.	Кол.уч	Лист	№ док.	Подп.	Дата
Разраб.		Кырлан А.С.			04.11.26
Пров.					
ГИП					
Н. контр.					
Утв.					

ГД-2026-010-АИ

Дом 331 м²

Общая площадь 270,67* м² · * размеры приняты, не замерены (реестр — л. 8–10, К-1)

Дизайн-проект интерьера	Стадия	Лист	Листов
	РП	213	216

Спецификация материалов (продолжение)

М б/м

Кырлан Александр Сергеевич

Спецификация материалов (окончание)

Отделочные материалы: чистое количество, запас, упаковка, к заказу · ГОСТ 21.110-2013

Спецификация материалов (ГОСТ 21.110-2013, форма 1) (продолжение)

Поз.	Наименование и техническая характеристика	Тип, марка, артикул	Код продукции	Поставщик	Ед. изм.	Количество				Масса ед., кг	Примечание
						чистое	запас, %	упаковка	к заказу		
34	Краска интерьерная акриловая, матовая, класс истирания 1	Farrow & Ball Modern Emulsion No. 64 «Red Earth»			л	1,76	10	банка 2,5 л	1 банк		7,35 м² × 2 сл. × 0,12 л/м²; пом. 16; л. 91–94
35	Краска интерьерная акриловая, матовая, класс истирания 2	Tikkurila Optiva 5 Matt S 3020-G30Y «S 3020-G30Y»			л	2,96	10	банка 2,7 л	2 банк		12,33 м² × 2 сл. × 0,12 л/м²; пом. 18; л. 91–94
36	Краска интерьерная акриловая, матовая, класс истирания 2	Tikkurila Optiva 5 Matt S 3040-Y70R «S 3040-Y70R»			л	3,56	10	банка 2,7 л	2 банк		14,85 м² × 2 сл. × 0,12 л/м²; пом. 19; л. 91–94
37	Шпаклёвка финишная полимерная под окраску (стены и потолки, Q3)	по выбору подрядчика			м²	897,26	10	ведро по ТУ	по ТУ		расход кг/м² на слой — по ТУ; л. 91–94
38	Грунтовка акриловая глубокого проникновения, 2 слоя	по выбору подрядчика			м²	970,13	10	канистра по ТУ	по ТУ		расход л/м² — по ТУ; л. 91–94
Погонажные изделия и потолки											
39	Плинтус напольный МДФ под покраску, h=80 мм, крепление к стене	аналог: плинтус МДФ под окраску 80×16 мм			м.п.	36,50	10	хлыст 2,4 м	17 шт		пом. 1, 5; длина хлыста — по артикулу; л. 91–94
40	Плинтус напольный МДФ под покраску, h=80 мм, крепление к стене	аналог: плинтус МДФ под покраску 80×16			м.п.	112,30	10	хлыст 2,4 м	52 шт		пом. 2, 4, 6, 7, 8, 9, 13, 14, 16, 17; длина хлыста — по артикулу; л. 91–94
41	Плинтус напольный ПВХ, h=100 мм, крепление к стене	аналог: плинтус ПВХ влагостойкий 100 мм, серый			м.п.	21,98	10	хлыст 2,4 м	11 шт		пом. 10; длина хлыста — по артикулу; л. 91–94
42	Керамогранит на плинтус: полосы h=80 мм из плитки пола, кромка с запилом 45°	аналог: плинтус из керамогранита пола, подрезка 80 мм, верхняя кромка с запилом 45°			м²	2,15	15	из партии пола	2,47 м²		26,84 м.п. × 0,08 м; пом. 11, 12; заказывать целыми плитками одной партии с полом, число плиток — по раскладке плиточника; л. 88, 89, 91–94
43	Плинтус напольный МДФ под покраску, h=69 мм, крепление к стене	SX165			м.п.	32,20	10	хлыст 2,4 м	15 шт		пом. 18, 19; длина хлыста — по артикулу; л. 91–94
44	Потолок подвесной ГКЛ/ГКЛВ по каркасу Knauf П113: листы, профили, подвесы, лента, шпаклёвка швов	Knauf П113			м²	202,89		комплект	по л. потолков		площадь — по ведомости потолков; число листов, профилей и подвесов — по шагам каркаса на листе потолков; л. 73–81

Примечания

1. Чистое количество — из ведомости объёмов работ и раскладки плитки; запас — отдельной графой (доска — по ведомости отделки, плитка, краска и плинтус — 10 %); «к заказу» — с запасом и кратно упаковке.
2. Плитка — штуками по раскладке, запас на каждую поверхность. Калибр (рабочий размер) и тон — одной партией на помещение, калибр указать при заказе и сверить с раскладкой до укладки.
3. Краска — 0,12 л/м² на слой (середина вилки 0,10–0,15 л/м²) по фактической площади окраски из ведомости отделки; колеровка одной партией.
4. «По ТУ» — расход задаёт производитель выбранного продукта; количество к заказу — после выбора марки.
5. Поз. 3, 39, 40, 41, 42 заданы характеристиками («аналог:»): марку, артикул и поставщика согласовать с заказчиком до закупки, без артикула не заказывать.
6. Штукатурная смесь — на ту же площадь, что строка ВОР «Штукатурка стен» (674,24 м²): площадь одна, расход смеси задаёт производитель.
7. Коробы инсталляции и стояков: ГКЛВ в 2 слоя и профиль 27 × 28 мм считаются по свободным граням коробов (источник — раскладка плиточника и шахты в данных); короб К1 над полом — в спецификации ВК.
8. Потолки ГКЛ: в этой спецификации — площадь системы П113; число листов, профилей и подвесов — по шагам каркаса на листе потолков (подвесы через 1000, несущие через 500, основные через 1200 мм), схема каркаса не выпущена. Сантехника, светильники и мебель — по своим спецификациям.

Допущения и предложения на листе

Основа листа: размеры и контуры этажей подобраны проектировщиком по составу помещений и площадям этажей с картинки 470 px (размеры на ней не читаются); обмер и исходный проект — задание (К-1); высоты: 1-й этаж 2800 мм, мансарда 2700 мм (горизонтальная часть) приняты; скаты кровли мансарды приняты по картинке: колено 1200 мм, уклон 45°, конёк вдоль длинной стороны; проект КР — задание (К-2); наружные стены 400 мм, перегородки 120 мм приняты (К-1); разрешённая мощность 15 кВт принята по типовым ТУ для частного дома (К-4); подрайон климата не задан — принят не северный (жилые от 2,5 м) (К-7).

Знак «*» — принято, не замерено и не подтверждено (замерить на объекте): К-13: пол пом. 11, 12 — отметка верха плиты −0,170 принята по пирогу (плита веранды и крыльца своя, ниже плиты дома) — подтвердить по проекту КР или обмером (К-13).

Знак «**» — предложение проектировщика, заказчиком не утверждено (согласовать с заказчиком): плинтус пом. 1, 2, 4–14, 16, 17, фартук пом. 1, акцент пом. 5 — артикул изделия не выбран: позиция описана характеристиками («аналог по характеристикам»), артикул выбирается при закупке; пол пом. 3, 15, 20 — пирог пола: стяжка 33 мм и обмазочная гидроизоляция добавлены разработчиком проекта; артикул изделия не выбран: позиция описана характеристиками («аналог по характеристикам»), артикул выбирается при закупке; пол пом. 10 — покрытие пола гаража — предложение исполнителя: выдерживает шины, масло и антигололёдные реагенты, без швов.

См. лист открытых вопросов (лист 8, записи К-1, К-2, К-4, К-7; лист 9, запись К-13).

Изм.	Кол.уч	Лист	№ док.	Подп.	Дата
Разраб.		Кырлан А.С.			04.11.26
Пров.					
ГИП					
Н. контр.					
Утв.					

ГД-2026-010-АИ

Дом 331 м²

Общая площадь 270,67* м² · * размеры приняты, не замерены (реестр — л. 8–10, К-1)

Дизайн-проект интерьера	Стадия	Лист	Листов
	РП	214	216
Спецификация материалов (окончание) М б/м	**Кырлан Александр Сергеевич**		

Смета ориентировочная

ПРЕДВАРИТЕЛЬНО · не для производства работ · открыто пунктов: 15 (реестр — л. 8–10)

Работы, материалы, оборудование, услуги и резерв · цены — ориентир по открытым прайсам, не коммерческое предложение

Сводная смета (прайсы собраны 21.09.2026, часть расценок сверена повторно 24.09.2026, Москва)

№	Наименование работ, материалов, услуг	Ед. изм.	Кол-во	Цена за ед., ₽	Стоимость, ₽			Чей подряд	Срок поставки, дн.	Основание	Источник цены
					план	факт	разница				
Работы — по ведомости объёмов работ											
1	Демонтаж и черновые работы (без 6 поз. по КП)	раздел	1		838 166			бригада, поставщик		ВОР, поз. 1–11; л. 207–211	по ВОР
2	Инженерные системы (без 13 поз. по КП)	раздел	1		328 130			бригада		ВОР, поз. 12–35; л. 207–211	по ВОР
3	Чистовые работы (без 1 поз. по КП)	раздел	1		1 938 641			бригада, поставщик		ВОР, поз. 36–55; л. 207–211	по ВОР
Материалы — по спецификации материалов											
4	Инженерная доска	м²	203,40	4 513	917 944			поставщик		спецификация, поз. 1	Ц7
5	Керамогранит 600×600 мм	м²	22,32	1 800	40 176			поставщик		спецификация, поз. 3	Ц6
6	Керамогранит 600×1200 мм	м²	163,44	3 500	572 040			поставщик		спецификация, поз. 4	Ц6
7	Клей плиточный цементный класса C2 TE S1	меш.	44	1 800	79 200			поставщик		спецификация, поз. 5	Ц7
8	Затирка цементная класса CG2WA	упак.	6	1 000	6 000			поставщик		спецификация, поз. 6	Ц7
9	Краска Tikkurila (Luja 7, Optiva 5 Matt, Anti-Reflex 2), банка 2,7 л	банк	30	3 510	105 300			поставщик		спецификация, поз. 23, 24, 30, 31, 33, 35, 36	Ц6
10	Краска Farrow & Ball Modern Emulsion, банка 2,5 л	банк	40	5 800	232 000			поставщик		спецификация, поз. 25, 26, 29, 34	Ц7
11	Плинтус напольный МДФ под покраску	шт	84	368	30 912			поставщик		спецификация, поз. 39, 40, 43	Ц7
12	Керамогранит на плинтус: полосы h=80 мм из плитки пола	м²	2,47	1 800	4 446			поставщик		спецификация, поз. 42	Ц6
13	Прочие материалы с расходом по ТУ (клей для доски, гидроизоляция, демпферная лента, смесь для стяжки, смесь штукатурная гипсовая для машинного и ручного нанесения по маякам, лист гклв 12, профиль стальной оцинкованный 27 × 28 мм: каркас коробов (стойки и направляющие), кабель слаботочки, гофра слаботочки, изделия слаботочки, краска, шпаклёвка, грунтовка, плинтус, каркас и ГКЛ потолков)	компл	1	по КП				поставщик		спецификация, поз. 2, 7, 8, 9, 10, 11, 12, 13, 14, 15, 16, 17, 18, 19, 20, 21, 22, 27, 28, 32, 37, 38, 41, 44	
Оборудование и мебель — поставка по спецификациям											
14	Кухонный гарнитур по проекту кухни, изготовление и монтаж (4–8 нед.)	компл	1	по КП				поставщик	не задан; ориентир 4–8 нед. от замера	л. 119, 120	
15	Двери скрытого монтажа с коробом под покраску, поставка	шт	9	по КП				поставщик	не задан; ориентир ≈ 30 дн.	л. 23–26	

Допущения и предложения на листе

Основа листа: размеры и контуры этажей подобраны проектировщиком по составу помещений и площадям этажей с картинки 470 px (размеры на ней не читаются); обмер и исходный проект — задание (К-1); высоты: 1-й этаж 2800 мм, мансарда 2700 мм (горизонтальная часть) приняты; скаты кровли мансарды приняты по картинке: колено 1200 мм, уклон 45°, конёк вдоль длинной стороны; проект КР — задание (К-2); наружные стены 400 мм, перегородки 120 мм приняты (К-1); разрешённая мощность 15 кВт принята по типовым ТУ для частного дома (К-4); подрайон климата не задан — принят не северный (жилые от 2,5 м) (К-7).

См. лист открытых вопросов (лист 8, записи К-1, К-2, К-4, К-7).

Изм.	Кол.уч	Лист	№ док.	Подп.	Дата
Разраб.		Кырлан А.С.			04.11.26
Пров.					
ГИП					
Н. контр.					
Утв.					

ГД-2026-010-АИ

Дом 331 м²

Общая площадь 270,67* м² · * размеры приняты, не замерены (реестр — л. 8–10, К-1)

Дизайн-проект интерьера	Стадия	Лист	Листов
	РП	215	216

Смета ориентировочная

М б/м

Кырлан Александр Сергеевич

Смета ориентировочная (окончание)

Работы, материалы, оборудование, услуги и резерв · цены — ориентир по открытым прайсам, не коммерческое предложение

Сводная смета (прайсы собраны 21.09.2026, часть расценок сверена повторно 24.09.2026, Москва) (продолжение)

№	Наименование работ, материалов, услуг	Ед. изм.	Кол-во	Цена за ед., ₽	Стоимость, ₽			Чей подряд	Срок поставки, дн.	Основание	Источник цены
					план	факт	разница				
16	Двери межкомнатные, поставка	шт	4	по КП				поставщик		л. 23–26	
17	Оборудование заказчика слаботочных сетей: точка доступа wi-fi — 1 шт; коммутатор — 1 шт	компл	1	по КП				заказчик		л. 43–45	
18	Сантехника, светильники, мебель и предметы интерьера	компл	1	по КП				поставщик		л. 70; л. 71, 72; л. 124; л. 32–36	
Прочие работы и услуги											
19	Вынос и вывоз строительного мусора	м³		по факту				бригада		после демонтажа	
20	Подъём материалов на этаж (лифтом или вручную — по договору)	т		по факту				бригада		по массе поставки	
21	Доставка чистовых материалов, 10 % от поставки			10 %	198 802			поставщик		от суммы материалов	
22	Уборка после ремонта	м²	270,67	по факту				бригада		S квартиры	
	Итого работы				**3 104 937**						
	Итого материалы				**1 988 018**						
	Итого прочие услуги				**198 802**						
	Резерв на непредвиденные работы и материалы, 15 %				**793 764**						
	ВСЕГО ориентировочно (без оборудования и позиций по КП)				**6 085 521**						

Примечания

1. Смета ориентировочная, не коммерческое предложение: объёмы — из ведомости объёмов работ и спецификации материалов, цены — нижняя граница открытых прайсов Москвы (прайсы собраны 21.09.2026, часть расценок сверена повторно 24.09.2026); перед договором цены подтвердить у подрядчика и поставщиков.
2. Источники цен: Ц1 — Домашний мастерок: прайс на отделочные работы, 2026; Ц2 — Домашний мастерок: прайс на плиточные работы, 2026; Ц3 Домашний мастерок: прайс на электромонтажные работы, 2026; Ц4 — Профи ремонтник: штукатурно-малярные работы; Ц5 — Profi.ru: укладка керамогранита на стены, Москва 2026; Ц6 — knowledge/spec-materials.md, разд. 1 и 3: ориентир по сегментам; Ц7 — Розница Москвы, 09.2026: Лемана ПРО, KGSnab, официальный дилер Farrow & Ball.
3. Повторная сверка с прайсом: 24.09.2026 — плинтус из керамогранита, нарезка плинтуса из плитки; остальные расценки — по прайсам, собранным 21.09.2026.
4. В итог не вошли позиции «по КП» и «по факту»: оборудование и мебель, двери, материалы с расходом по ТУ, вывоз мусора, подъём и уборка.
5. Доставка — 10 % от материалов, резерв — 15 % (частный ремонт 10–20 %) отдельными строками, в количествах не спрятаны. Графы «факт» и «разница» заполняются по актам.

Допущения и предложения на листе

Основа листа: размеры и контуры этажей подобраны проектировщиком по составу помещений и площадям этажей с картинки 470 px (размеры на ней не читаются); обмер и исходный проект — задание (К-1); высоты: 1-й этаж 2800 мм, мансарда 2700 мм (горизонтальная часть) приняты; скаты кровли мансарды приняты по картинке: колено 1200 мм, уклон 45°, конёк вдоль длинной стороны; проект КР — задание (К-2); наружные стены 400 мм, перегородки 120 мм приняты (К-1); разрешённая мощность 15 кВт принята по типовым ТУ для частного дома (К-4); подрайон климата не задан — принят не северный (жилые от 2,5 м) (К-7).
См. лист открытых вопросов (лист 8, записи К-1, К-2, К-4, К-7).

Изм.	Кол.уч	Лист	№ док.	Подп.	Дата
Разраб.		Кырлан А.С.			04.11.26
Пров.					
ГИП					
Н. контр.					
Утв.					

ГД-2026-010-АИ

Дом 331 м²

Общая площадь 270,67* м² · * размеры приняты, не замерены (реестр — л. 8–10, К-1)

Дизайн-проект интерьера	Стадия	Лист	Листов
	РП	216	216

Смета ориентировочная (окончание)

М б/м

Кырлан Александр Сергеевич

выпуск 04.11.2026 № 2a77323a49 · стр. 221 из 221