
L

LINEA

ДИЗАЙН-ПРОЕКТ ИНТЕРЬЕРА

Дом 271 м²

Шале

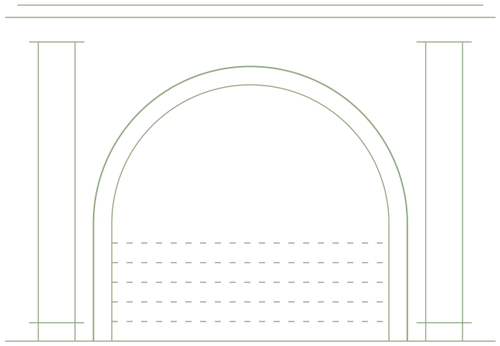


ПАЛИТРА ОТДЕЛКИ

F&B No. 226	Little Greene	NCS S 0804-Y30	NCS S 3040-Y70	F&B No. 93
37 %	30 %	26 %	2 %	1 %

АВТОР ПРОЕКТА

Кырлан Александр Сергеевич

Ноябрь 2026

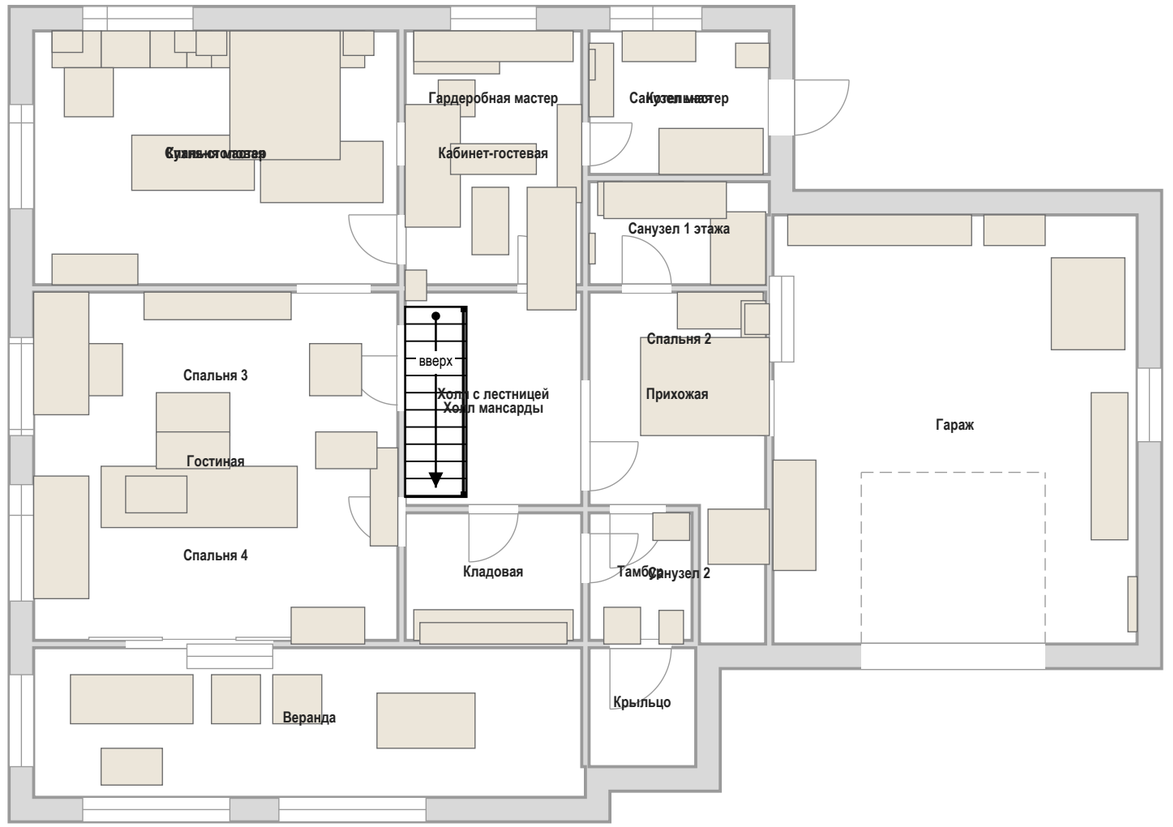

План расстановки мебели · М 1:100

ОБЩАЯ ПЛОЩАДЬ	ПОМЕЩЕНИЙ	СТАДИЯ	ШИФР	ОСНОВА
270,67 м²	20, из них жилых 6	Проект · предварительно	ГД-2026-010-АИ	план заказчика, без обмера

Как оставить правку: кнопка «Правка к этому листу» в правом верхнем углу любого листа · все листы проекта: дизайн-студия-квартир.рф/review.html?p=gost-dom331

выпуск 04.11.2026 № f163a372b2 · стр. 1 из 168

Объект

Дом 331 м²: 295,89 м², помещений 20, из них жилых 6.

Стиль: шале 60 %, эко и органический модерн 40 %. Стадия: предварительный альбом без обмера, планировка по плану заказчика.

Открытых вопросов 12, конфликтов разделов 1; изменений утверждено 0, ждут подписи 2.

Розетки и выводы

69 розеток (рамок 62), 9 выводов кабеля под технику и свет, 21 группа щита — всё с высотами от чистого пола: листы 57, 58.

Что решено (подписано вами)

Подписанных решений пока нет.

Что ждёт вашего ответа

К-1 — Размеры дома на картинке заказчика (470 px) не читаются: состав помещений и форма сняты с картинки, размеры подобраны проектировщиком под площади этажей 185,80 и 145,73 м².

К-2 — Высоты этажей и кровля не известны: приняты 2800 мм (1-й этаж) и 2700 мм (горизонтальная часть потолка мансарды).

К-4 — Разрешённая мощность дома по ТУ неизвестна, принята 15 кВт.

К-5 — Планировка этажей по составу помещений с картинки (несущие стены, лестница, перекрытие не известны): нужен проект АР/КР дома.

К-6 — Лестница Л-1 на картинке заказчика — одномаршевая в холле 1-го этажа (3,0×3,6 м), видно 11 проступей.

К-7 — Климатический подрайон (СП 131.13330) не задан: принят не северный — жилые комнаты и кухня под потолком от 2,5 м (СП 54, п. 5.12).

К-8 — Душ С_01 с трапом (санузел 1-го этажа): в стяжке 35 мм трап не встаёт — монтажная высота трапа ≈ 90 мм (по паспорту модели) + уклон отвода Ø50 до стояка Ст К1-1 (1,70 м × 25…

К-9 — Дверь Д-4 гостиной (пом. 5) на террасу, проём 2400 × 2100, остеклённая: число полотен и ширина полотна в данных не заданы (ряд полотен — до 1200 мм), толщина и класс…

К-10 — Кухня-столовая (пом. 1): мойка М_01 и модули М_06, М_02 стоят под окном 1400 × 1500 стены А с низом проёма +0,900 — подоконник в уровне столешницы (+0,900).

К-11 — Тип котла (газ / электро / твёрдое топливо) и его мощность не выбраны.

К-12 — Вентканалы ВК-1…ВК-3 приняты проектировщиком (на картинке заказчика не показаны).

К-13 — Веранда (пом. 11) и крыльцо (пом. 12): чистый пол −0,030, пирог 140 мм (утеплитель XPS 100, сборное основание ГВЛВ 25, клей 5, керамогранит 10) — верх плиты принят −0,170, то…

Кф-1 — Кухня-столовая (пом. 1): радиатор РО-1 под окном стены А (800…2200, выведен листом ОВ по оси окна) попадает в объём нижних модулей М_06 (300…1100), М_01 (мойка, 1100…1900) и…

Предложено, ждёт подписи

ИЗ-1 — Веранда — линия L12, выключатель S30 в гостиной у двери Д-4.

ИЗ-2 — РО-1 — на свободном участке наружной стены Г у угла со стеной В: привязка 3500, 600 × 600, низ +120.

					Проект: Дом 331 м²
	Лист	№ док.	Подпись	Дата	Ваш проект на одной странице
Дизайнер	Кырлан А.С.			04.11.26	

Стадия	Лист	Листов
П	2	168

Список листов

Лист	Наименование
1	Титульный лист
2	Ваш проект на одной странице
3	Список листов
4	Список листов
5	Как читать альбом
6	План планировки от заказчика · 1-й этаж
7	План планировки от заказчика · Мансарда
8	План монтажный · 1-й этаж
9	План монтажный · Мансарда
10	Кухня (пом. 1). Монтажная схема
11	Шкафы. Монтажная схема. Лист 1 из 2
12	Шкафы. Монтажная схема. Лист 2 из 2
13	Карта покрытий стен · 1-й этаж
14	Карта покрытий стен · Мансарда
15	Колерная карта
16	Колерная карта
17	План размещения мебели и оборудования · 1-й этаж
18	План размещения мебели и оборудования · Мансарда
19	Спецификация мебели и оборудования
20	Спецификация мебели и оборудования (продолжение)
21	Спецификация мебели и оборудования (продолжение)
22	Спецификация мебели и оборудования (продолжение)
23	Спецификация мебели и оборудования (продолжение)
24	Ведомости изделий, техники и фурнитуры
25	План выводов сантехники · 1-й этаж
26	План выводов сантехники · Мансарда
27	Схема разводки водопровода и канализации · 1-й этаж
28	Схема разводки водопровода и канализации · Мансарда
29	Аксонометрическая схема В1 (холодное водоснабжение)
30	Аксонометрическая схема Т3 (горячее водоснабжение)
31	Аксонометрическая схема К1 (канализация)
32	Развёртки мокрых зон: выводы ВК. Кухня-столовая
33	Развёртки мокрых зон: выводы ВК. Санузел 1 этажа (лист 1 из 2)
34	Развёртки мокрых зон: выводы ВК. Санузел 1 этажа (лист 2 из 2)
35	Развёртки мокрых зон: выводы ВК. Санузел мастер (лист 1 из 2)
36	Развёртки мокрых зон: выводы ВК. Санузел мастер (лист 2 из 2)
37	Развёртки мокрых зон: выводы ВК. Санузел 2 (лист 1 из 2)
38	Развёртки мокрых зон: выводы ВК. Санузел 2 (лист 2 из 2)
39	Спецификация сантехнического оборудования
40	Раскладка плитки. Санузел 1 этажа. Развёртки стен
41	Раскладка плитки. Санузел мастер. Развёртки стен
42	Раскладка плитки. Санузел 2. Развёртки стен
43	План размещения дверей · 1-й этаж
44	План размещения дверей · Мансарда
45	Ведомость заполнения проёмов
46	Схемы дверных блоков
47	Лестница Л-1
48	План потолков · 1-й этаж
49	План потолков · Мансарда
50	Разрезы и узлы потолков
51	Разрезы и узлы потолков (продолжение)
52	Разрезы и узлы потолков (продолжение)
53	Разрезы и узлы потолков (продолжение)
54	Сечения потолков М 1:10
55	Сечения потолков М 1:10
56	Сечения потолков М 1:10
57	Однолинейная схема щита
58	Однолинейная схема щита (продолжение)
59	План розеток и электровыводов · 1-й этаж
60	План розеток и электровыводов · Мансарда
61	План слаботочных сетей · 1-й этаж
62	План слаботочных сетей · Мансарда
63	План освещения · 1-й этаж
64	План освещения · Мансарда
65	Техническое задание на подбор светильников
66	Техническое задание на подбор светильников (продолжение)
67	Управление светильниками · 1-й этаж
68	Управление светильниками · Мансарда
69	План вентиляции · 1-й этаж
70	План вентиляции · Мансарда
71	План отопления · 1-й этаж
72	План отопления · Мансарда
73	План покрытий пола · 1-й этаж
74	План покрытий пола · Мансарда
75	Раскладка плитки. Планы полов
76	Раскладка плитки. Котельная. Прихожая. Тамбур
77	Развёртка стены А. Кухня-столовая (пом. 1), кухонный фронт
78	Привязки электроточек и выводов ВК, стена А. Кухня-столовая (пом. 1)
79	Развёртка стены Б. Кухня-столовая (пом. 1)
80	Развёртка стены В. Кухня-столовая (пом. 1)
81	Развёртка стены Г. Кухня-столовая (пом. 1)
82	Развёртка стены А. Кабинет-гостевая (пом. 2)
83	Развёртка стены Б. Кабинет-гостевая (пом. 2)
84	Развёртка стены В. Кабинет-гостевая (пом. 2)

					Проект: Дом 331 м²
	Лист	№ док.	Подпись	Дата	
Дизайнер	Кырлан А.С.			04.11.26	Список листов
					Стадия: П; Лист: 3; Листов: 168

Список листов (продолжение)

Лист	Наименование
85	Привязки электроточек, стены А, В. Кабинет-гостевая (пом. 2)
86	Развёртка стены Г. Кабинет-гостевая (пом. 2)
87	Развёртки стен А, Б. Санузел 1 этажа (пом. 3)
88	Привязки выводов ВК, стена А. Санузел 1 этажа (пом. 3)
89	Развёртки стен В, Г. Санузел 1 этажа (пом. 3)
90	Развёртки стен А, Б. Котельная (пом. 4)
91	Развёртка стены Г. Котельная (пом. 4)
92	Развёртка стены А. Гостиная (пом. 5)
93	Привязки электроточек, стена А. Гостиная (пом. 5)
94	Развёртка стены Б. Гостиная (пом. 5)
95	Развёртка стены В. Гостиная (пом. 5)
96	Развёртка стены Г. Гостиная (пом. 5)
97	Развёртка стены А. Холл с лестницей (пом. 6)
98	Развёртка стены В. Холл с лестницей (пом. 6)
99	Развёртки стен. Кладовая (пом. 7)
100	Развёртка стены А. Прихожая (пом. 8)
101	Развёртка стены Б. Прихожая (пом. 8)
102	Развёртка стены В. Прихожая (пом. 8)
103	Развёртка стены Г. Прихожая (пом. 8)
104	Привязки электроточек, стена Г. Прихожая (пом. 8)
105	Развёртки стен. Тамбур (пом. 9)
106	Развёртка стены А. Гараж (пом. 10)
107	Развёртка стены Б. Гараж (пом. 10)
108	Развёртка стены В. Гараж (пом. 10)
109	Развёртка стены Г. Гараж (пом. 10)
110	Развёртка стены А. Веранда (пом. 11)
111	Развёртка стены В. Веранда (пом. 11)
112	Развёртка стены Г. Веранда (пом. 11)
113	Развёртки стен. Крыльцо (пом. 12)
114	Развёртка стены А. Спальня мастер (пом. 13)
115	Привязки электроточек, стена А. Спальня мастер (пом. 13)
116	Развёртка стены Б. Спальня мастер (пом. 13)
117	Развёртка стены В. Спальня мастер (пом. 13)
118	Развёртка стены Г. Спальня мастер (пом. 13)
119	Развёртки стен А, Б. Гардеробная мастер (пом. 14)
120	Развёртки стен В, Г. Гардеробная мастер (пом. 14)
121	Развёртки стен А, Б. Санузел мастер (пом. 15)
122	Развёртки стен В, Г. Санузел мастер (пом. 15)
123	Привязки электроточек и выводов ВК, стены А, В. Санузел мастер (пом. 15)
124	Развёртка стены А. Спальня 2 (пом. 16)
125	Развёртка стены Б. Спальня 2 (пом. 16)
126	Развёртка стены В. Спальня 2 (пом. 16)
127	Привязки электроточек, стены А, В. Спальня 2 (пом. 16)
128	Развёртка стены Г. Спальня 2 (пом. 16)
129	Развёртка стены А. Холл мансарды (пом. 17)
130	Развёртка стены Б. Холл мансарды (пом. 17)
131	Развёртка стены В. Холл мансарды (пом. 17)
132	Развёртка стены Г. Холл мансарды (пом. 17)
133	Развёртка стены А. Спальня 3 (пом. 18)
134	Развёртки стен Б, Г. Спальня 3 (пом. 18)
135	Развёртка стены В. Спальня 3 (пом. 18)
136	Привязки электроточек, стена В. Спальня 3 (пом. 18)
137	Развёртка стены А. Спальня 4 (пом. 19)
138	Развёртка стены Б. Спальня 4 (пом. 19)
139	Развёртка стены В. Спальня 4 (пом. 19)
140	Привязки электроточек, стена В. Спальня 4 (пом. 19)
141	Развёртка стены Г. Спальня 4 (пом. 19)
142	Развёртки стен А, Б. Санузел 2 (пом. 20)
143	Привязки электроточек и выводов ВК, стены А, Б. Санузел 2 (пом. 20)
144	Развёртки стен В, Г. Санузел 2 (пом. 20)
145	Привязки электроточек и выводов ВК, стена В. Санузел 2 (пом. 20)
146	Открытые вопросы, принятые допущения и конфликты. Лист 1 из 2
147	Открытые вопросы, принятые допущения и конфликты. Лист 2 из 2
Д_1	Система хранения M_17
Д_2	Система хранения M_23
Д_3	Шкаф-купе M_24
Д_4	Система хранения M_26
Д_5	Система хранения M_43
Д_6	Шкаф распашной M_46
Д_7	Система хранения M_49
Д_8	Шкаф распашной M_53
Д_9	Шкаф распашной M_56
Д_10	Кухня (пом. 1). Развёртка гарнитура
Д_11	Остров M_07 (пом. 1). Чертёж изделия
С1	Ведомость отделки помещений. Лист 1 из 4
С2	Ведомость отделки помещений. Лист 2 из 4
С3	Ведомость отделки помещений. Лист 3 из 4
С4	Ведомость отделки помещений. Лист 4 из 4
С5	Спецификация отделочных материалов
С6	Спецификация отделочных материалов
С7	Список покупок
С8	Список покупок (окончание)
С9	Узлы. Лист 1 из 2
С10	Узлы. Лист 2 из 2

Общие указания

1. Размеры даны в мм от чистовых поверхностей стен: слой штукатурки 20 мм по блоку и 5 мм шпаклёвки по ГКЛ учтён. Перед заказом встроенной мебели — контрольный обмер после штукатурки.
2. Привязки мебели — от стен и углов помещения, а не от другой мебели.
3. Розетки, выводы и выключатели под мебель — см. лист 59 «План розеток и электровыводов · 1-й этаж»; сантехприборы и выводы воды — лист 25.
4. План расстановки не является документацией для изготовления мебели: изделия — по чертежам мебельщика; покупную мебель заменять только на изделия не больше габарита из спецификации (лист 19).
5. Встроенная мебель «стена в стену» — с зазором 10 мм с каждой стороны или с компенсаторами.
6. Развёртки — вид на стену изнутри помещения, по часовой стрелке; расположение стен на схеме листа развёртки; размеры — в мм по чистовым поверхностям; отметки — в м от ±0,000 (чистый пол 1-го этажа); высоты H — от чистого пола помещения до оси изделия, у декора — до центра.
7. Красная цепочка — привязки электроточек и выводов по осям от угла чистовых стен; высота H — у знака, от чистого пола до оси; высоты мебели, проёмов и границ отделки колонкой отметок слева. Стена с 5 и более точками или с мелкими звеньями привязок показана двумя видами: архитектурная развёртка (мебель, отделка, проёмы, высоты) и вид «Привязки» на отдельном листе — точки и выводы с марками, одна цепочка по осям и таблица привязок (каждая точка — строка).
8. У знака электроточки: марка (Р — розетка, S — выключатель, Св — светильник, ЭВ вывод кабеля), ×N — число постов в рамке, гр. — группа щита, H — высота оси от чистого пола, мм; группы по клавишам выключателя — на листе выключателей.
9. Схема мебели, приборов и декора не является технической документацией для производства мебели; габариты — по паспортам изделий.
10. Марки позиций: M_NN — мебель, ОБ_NN — оборудование, С_NN — сантехника; О-N отделка (ведомость отделочных материалов, серия С).
11. Размеры мебели и изделий на заказ уточнить по месту после отделочных работ.

					Проект: Дом 331 м²
	Лист	№ док.	Подпись	Дата	Список листов
Дизайнер	Кырлан А.С.			04.11.26	Стадия: П · Лист: 4 · Листов: 168

Что в альбоме

Альбом — дизайн-проект с рабочими чертежами для ремонта. Листы идут в порядке работ: титул и вводные, реестр открытых вопросов и решений, планы (обмер, монтаж стен, мебель, двери, потолки, полы), инженерия (сантехника, электрика, вентиляция и отопление), развёртки стен с визуализациями помещений, чертежи мебели, ведомости материалов и узлы.

Вам как заказчику — титул, эта вводная, «Ваш проект на одной странице», реестр вопросов, план мебели, визуализации и развёртки, ведомости мебели и материалов. Подрядчику — всё остальное: монтажные планы, привязки выводов и розеток, узлы, ведомости объёмов.

Знаки на листах

Без знака — решение утверждено или подтверждено обмером.

Что проверить до ремонта

1. Розетки у кровати и рабочего места: хватает ли их с каждой стороны кровати и над столом (план розеток — листы электрики).

2. Выводы под технику — варочная панель, духовка, посудомойка, стиральная машина, бойлер: совпадают ли с выбранными моделями (листы 19, 20, 21, 22, 23).

3. Высоты розеток, выключателей и выводов даны от чистого пола: если мебель или техника будут другими — скажите до штробления стен.

Номера записей

К-N — открытый вопрос: чего не хватает или что выбрать (варианты и рекомендация — в тексте). Пока ответа нет, действует строка «если решения нет».

Кф-N — конфликт между разделами (например, мебель и радиатор в одном месте); закрывается решением, которое записывается как ИЗ-N.

ИЗ-N — изменение проекта: что было, что стало и кто утвердил. Изменение без подписи предложение.

Все записи — на листе реестра сразу после вводных; на других листах на них стоят ссылки.

Почему альбом предварительный


Обмера на объекте не было: размеры взяты с плана заказчика. Технические условия (мощность, вода, вентиляция дома) не получены, часть решений ждёт вашего ответа. Пока в реестре есть открытые вопросы, альбом предварительный — пометка в штампе снимается закрытием вопросов, а не стиранием.

Правку к любому листу можно оставить по кнопке «Правка к листу» или на сайте студии: дизайн-студия-квартир.рф — укажите номер листа и что изменить.

3 круга правок входят в цену; условия — в договоре и на странице вашего заказа на сайте студии.

Отметки по высоте

±0,000	чистый пол пом. 1, 2, 4–10; отсчёт высот
−0,015	чистый пол пом. 3, ниже на 15 мм
−0,030	чистый пол пом. 11, 12, ниже на 30 мм
плита	верх плиты разный: −0,064, −0,170 (задание на обмер)
сущ. пол	снимается до плиты; не замерен (задание на обмер)

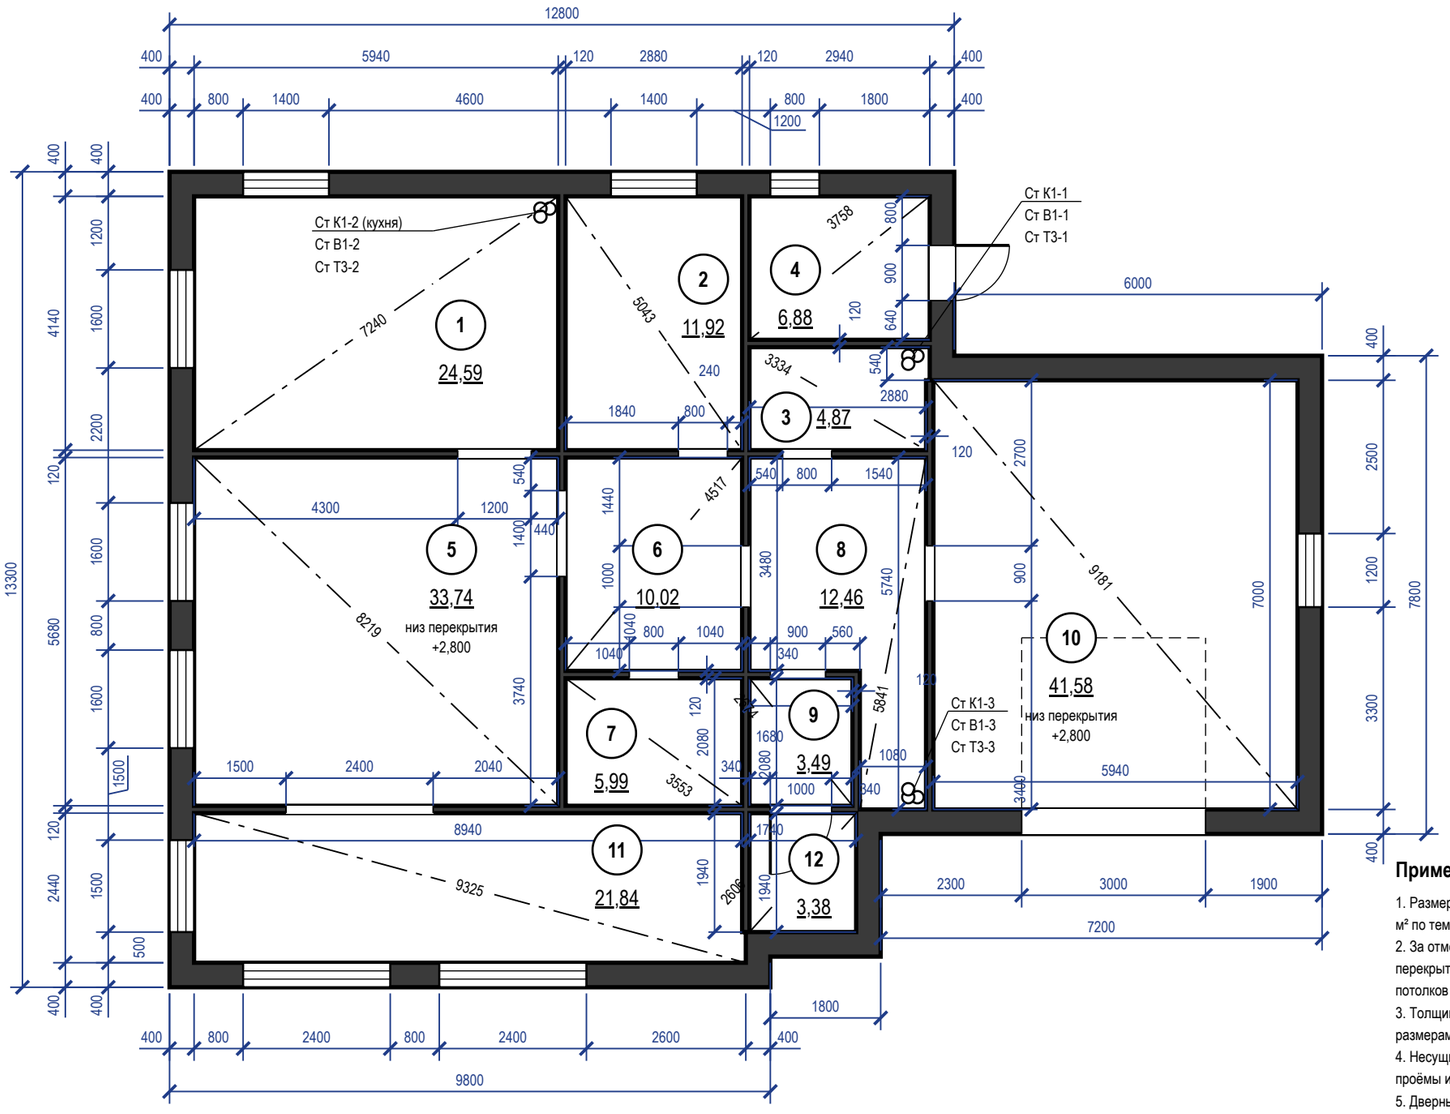

Экспликация помещений

№	Наименование	Площадь, м²
1	Кухня-столовая	24,59
2	Кабинет-гостевая	11,92
3	Санузел 1 этажа	4,87
4	Котельная	6,88
5	Гостиная	33,74
6	Холл с лестницей	10,02
7	Кладовая	5,99
8	Прихожая	12,46
9	Тамбур	3,49
10	Гараж	41,58
11	Веранда *	21,84
12	Крыльцо *	3,38
	Итого по этажу	**155,54**
	Итого по дому	**270,67**


Условные обозначения

- существующие стены (сечение)
- окно (рама, остекление)
- проём существующий, без заполнения (откосы)
- стояк: К1 — канализация, В1 — ХВС, Т3 — ГВС
- диагональ помещения — контроль прямоугольности
- (1) номер помещения, площадь м²

Примечания

1. Размеры — в мм по чистым поверхностям стен до отделки (по плану заказчика); площади — в м² по тем же размерам. До начала работ выполнить контрольный обмер.
2. За отметку ±0,000 принят чистый пол 1-го этажа, не существующий (блок отметок). «Низ перекрытия» у марки помещения — отметка низа перекрытия от ±0,000, как на развёртках и плане потолков (не высота потолка: потолок — по плану потолков).
3. Толщины стен: наружные 400 мм, перегородки 120 мм; отличающиеся толщины и уступы размерами на плане.
4. Несущие стены не определены: до технического заключения все стены считать несущими; проёмы и штробы в них не выполнять.
5. Дверные проёмы показаны без заполнения (двери — лист 45); высота дверных проёмов 2100, 2300 мм, проёмов без двери 2100 мм; низ окон (подоконник) 900, 1200 мм от чистого пола, высота окон 1500, 900, 1600 мм.
6. Диагонали — контрольные размеры; расхождение более 5 мм подписать на плане как перекос.
7. Размеры проверить на месте до начала работ; расхождение контрольных промеров ≤ 2 %.
8. Помещения, отмеченные *, в общую площадь дома и в итоги не входят.

					Проект: Дом 331 м²	**М 1:100**
	Лист	№ док.	Подпись	Дата	План планировки от заказчика · 1-й этаж	Стадия / Лист / Листов
Дизайнер	Кырлан А.С.			04.11.26		П / 6 / 168

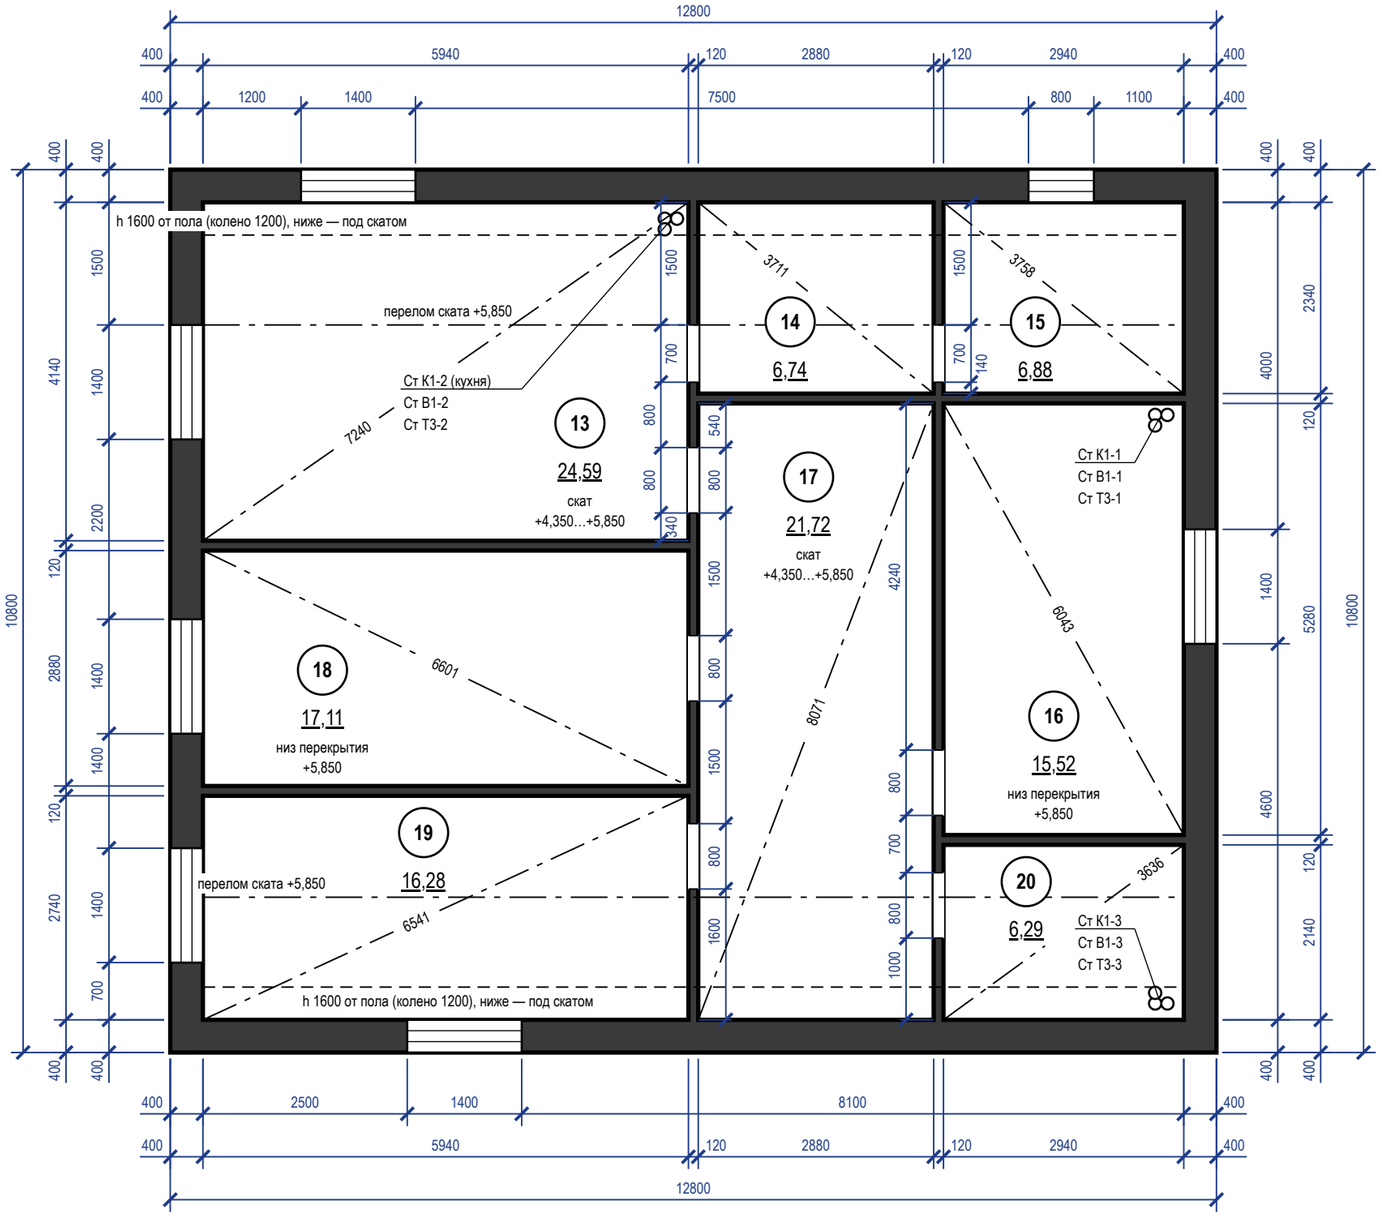

Экспликация помещений

№	Наименование	Площадь, м²
13	Спальня мастер	24,59
14	Гардеробная мастер	6,74
15	Санузел мастер	6,88
16	Спальня 2	15,52
17	Холл мансарды	21,72
18	Спальня 3	17,11
19	Спальня 4	16,28
20	Санузел 2	6,29
	Итого по этажу	**115,13**

Условные обозначения

- существующие стены (сечение)
- окно (рама, остекление)
- проём существующий, без заполнения (откосы)
- стояк: К1 — канализация, В1 — ХВС, Т3 — ГВС
- диагональ помещения — контроль прямоугольности
- (1) номер помещения, площадь м²

Примечания

1. Размеры — в мм по чистым поверхностям стен до отделки (по плану заказчика); площади — в м² по тем же размерам. До начала работ выполнить контрольный обмер.
2. За отметку ±0,000 принят чистый пол 1-го этажа, не существующий; чистый пол этажа +3,150 (блок отметок). «Низ перекрытия» у марки помещения — отметка низа перекрытия от ±0,000, как на развёртках и плане потолков (не высота потолка: потолок — по плану потолков).
3. Толщины стен: наружные 400 мм, перегородки 120 мм; отличающиеся толщины и уступы размерами на плане.
4. Несущие стены не определены: до технического заключения все стены считать несущими; проёмы и штробы в них не выполнять.
5. Дверные проёмы показаны без заполнения (двери — лист 45); высота дверных проёмов 2100 мм; низ окон (подоконник) 900, 1500 мм от чистого пола, высота окон 1500, 800 мм.
6. Диагонали — контрольные размеры; расхождение более 5 мм подписать на плане как перекос.
7. Размеры проверить на месте до начала работ; расхождение контрольных промеров ≤ 2 %.

Отметки по высоте


±0,000	чистый пол 1-го этажа; отсчёт отметок
+3,150	чистый пол пом. 13, 14, 16–19 (мансарда)
+3,135	чистый пол пом. 15, 20, ниже на 15 мм
+3,086	верх плиты — расчёт, не замер (задание на обмер)
сущ. пол	снимается до плиты; не замерен (задание на обмер)

	Лист	№ док.	Подпись	Дата
Дизайнер	Кырлан А.С.			04.11.26

Проект: Дом 331 м² — **М 1:75**

План планировки от заказчика · Мансарда

Стадия	Лист	Листов
П	7	168

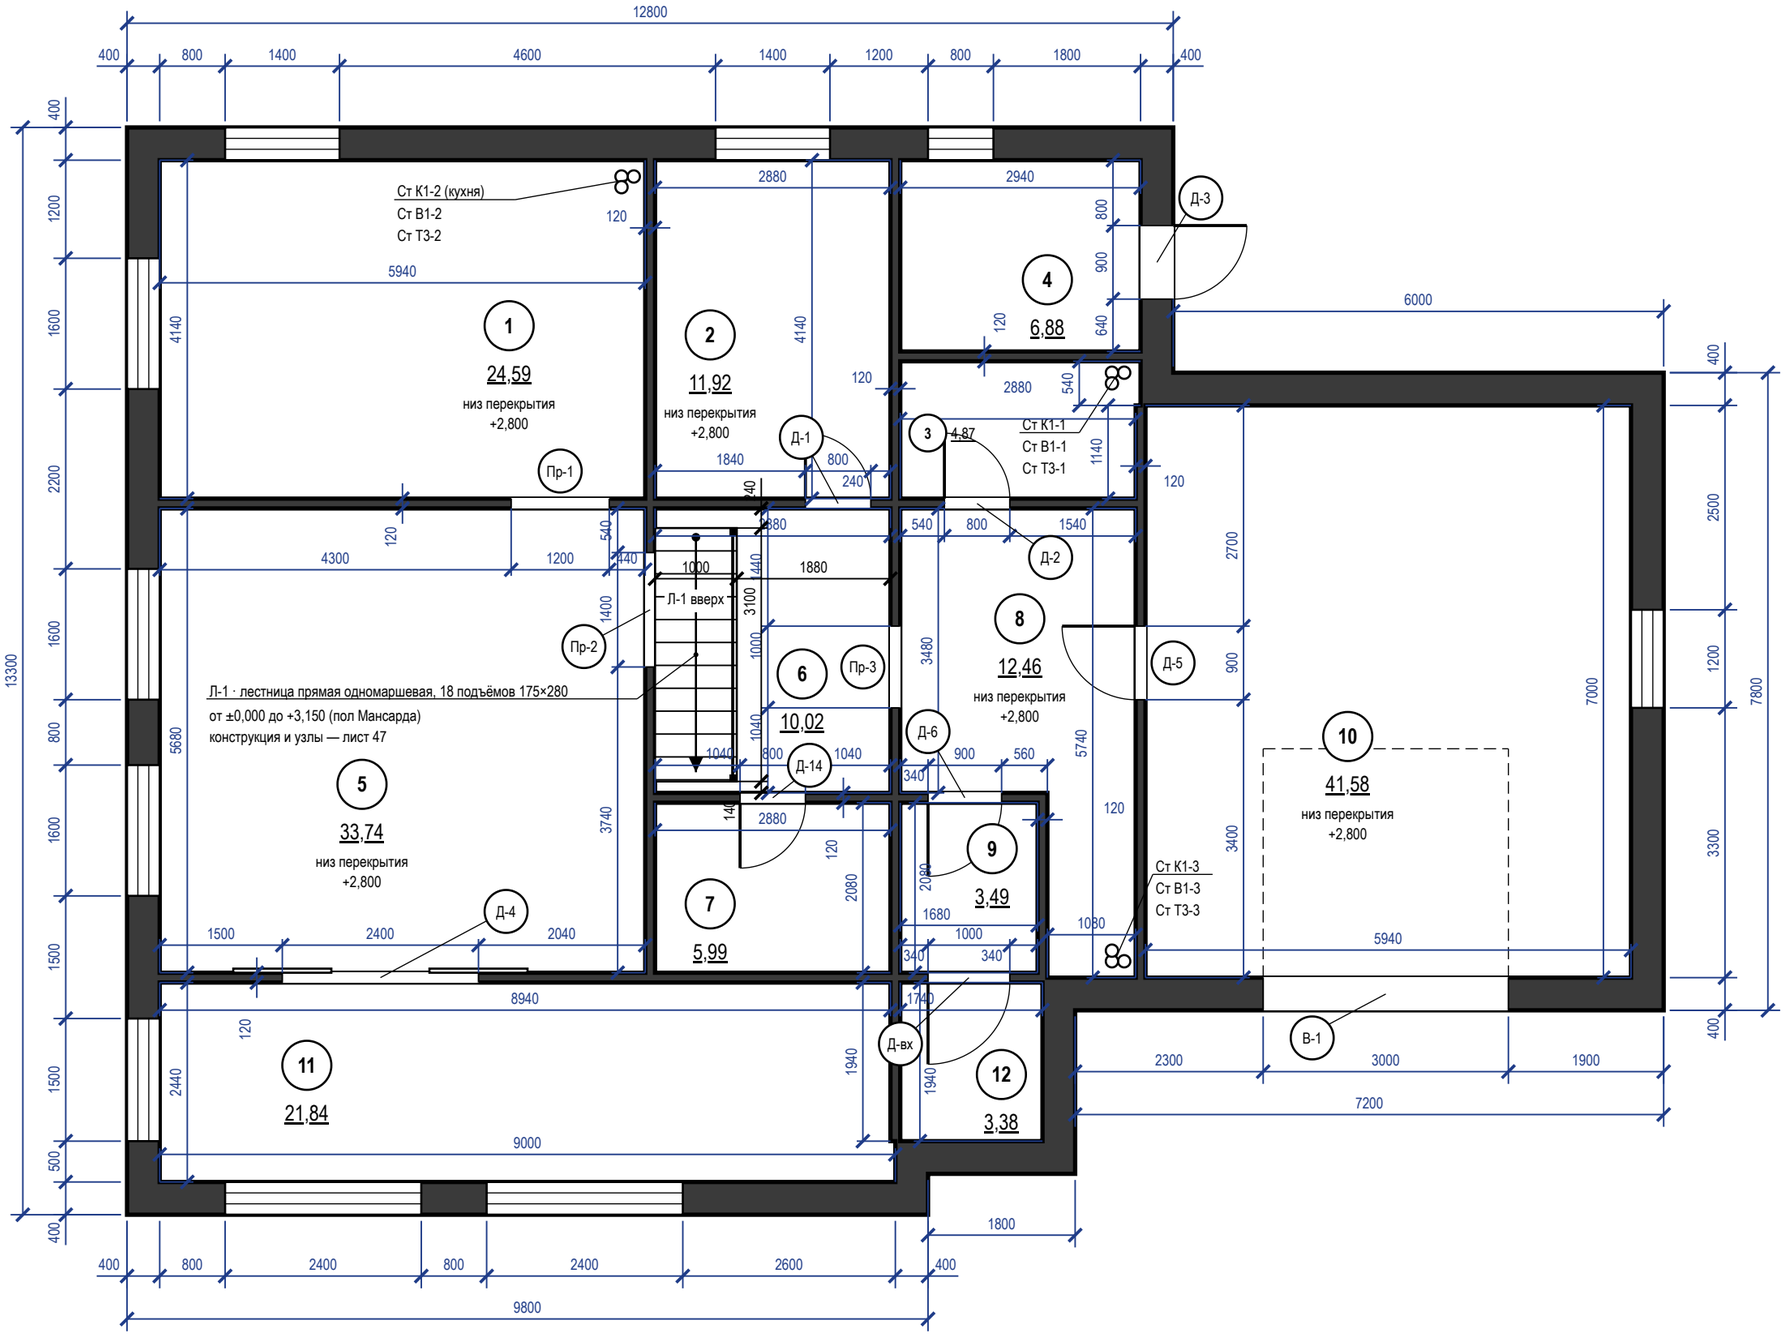

Экспликация помещений

№	Наименование	Площадь, м²
1	Кухня-столовая	24,59
2	Кабинет-гостевая	11,92
3	Санузел 1 этажа	4,87
4	Котельная	6,88
5	Гостиная	33,74
6	Холл с лестницей	10,02
7	Кладовая	5,99
8	Прихожая	12,46
9	Тамбур	3,49
10	Гараж	41,58
11	Веранда *	21,84
12	Крыльцо *	3,38
	Итого по этажу	**155,54**
	Итого по дому	**270,67**


Таблица проёмов

Марка	Наименование	Проём ш×в, мм	Полотно (расч.)
Д-вх	Дверь входная	1000×2100	блок — задать
В-1	Дверь	3000×2300	не задано (записи реестра нет)
Д-1	Дверь скрытого монтажа	800×2100	700×2000
Д-2	Дверь скрытого монтажа	800×2100	700×2000
Д-3	Дверь входная	900×2100	блок — задать
Д-4	Дверь раздвижная	2400×2100	не задано (записи реестра нет)
Д-5	Дверь распашная	900×2100	800×2000
Д-6	Дверь распашная	900×2100	800×2000
Д-14	Дверь распашная	800×2100	700×2000
Пр-1	Проём без заполнения	1200×2100	
Пр-2	Проём без заполнения	1400×2100	
Пр-3	Проём без заполнения	1000×2100	

Примечания

1. Размеры — в мм от чистовых поверхностей стен до отделки; размеры уточнить по месту до начала работ.
2. Д-N, ПР-N в кружке — марка проёма: проём и полотно — по таблице проёмов, «расч.» — полотно по проёму, заказ — по выбранной модели; ведомость, отделка и фурнитура — лист 45.
3. Несущие стены не изменять: проёмы, ниши и штробы в них — только по техническому заключению.
4. «расч.» — полотно, выведенное из проёма по запасу каталогов; заказ — по таблице проёмов выбранной модели; Д-1, Д-2: проём 2100, а под полотно 2000 по каталогам нужен 2050–2080, под 2100 — 2150–2180: высоту проёма — по модели; Д-5, Д-6, Д-14: проём 2100, а под полотно 2000 по каталогам нужен 2040–2080, под 2100 — 2140–2180: высоту проёма — по модели; Д-вх: входной блок по ГОСТ 31173-2016 — задать при выборе блока; Д-3: входной блок по ГОСТ 31173-2016 задать при выборе блока; Д-4: раздвижная, полотно — по системе — полотно задать при выборе модели.

					Проект: Дом 331 м² — М 1:75
	Лист	№ док.	Подпись	Дата	План монтажный · 1-й этаж
Дизайнер	Кырлан А.С.			04.11.26	Стадия: П; Лист: 8; Листов: 168

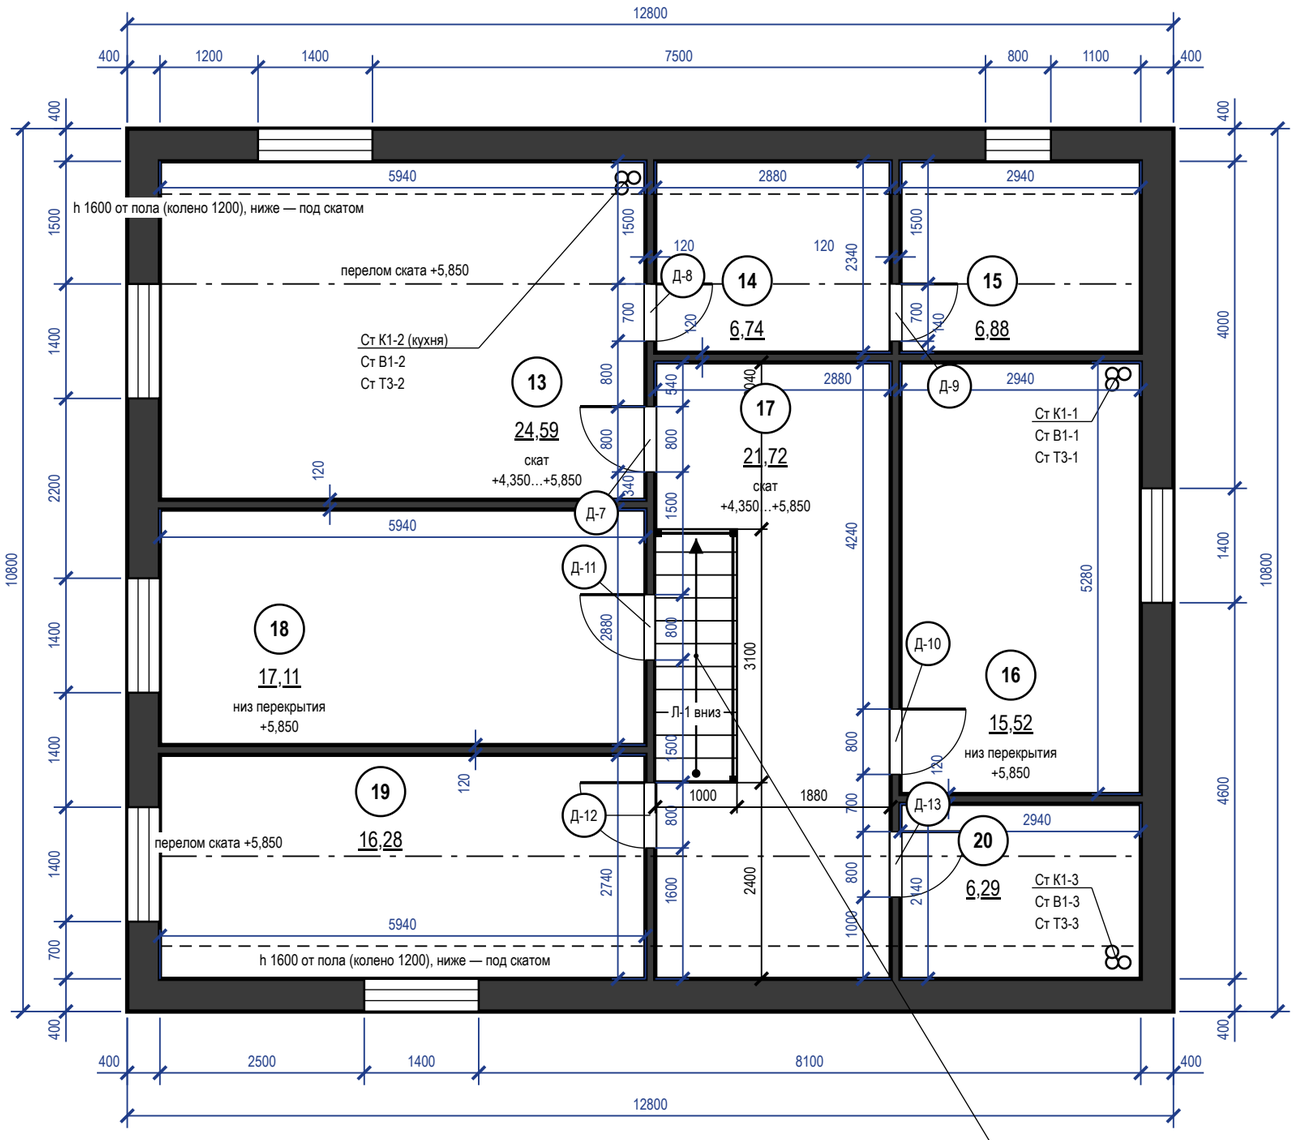

Проём в перекрытии 1000×3100 под Л-1

ограждение проёма h=900, балясины; пол +3,150

конструкция и узлы — лист 47

Экспликация помещений

№	Наименование	Площадь, м²
13	Спальня мастер	24,59
14	Гардеробная мастер	6,74
15	Санузел мастер	6,88
16	Спальня 2	15,52
17	Холл мансарды	21,72
18	Спальня 3	17,11
19	Спальня 4	16,28
20	Санузел 2	6,29
	Итого по этажу	**115,13**

Таблица проёмов

Марка	Наименование	Проём ш×в, мм	Полотно (расч.)
Д-7	Дверь скрытого монтажа	800×2100	700×2000
Д-8	Дверь скрытого монтажа	700×2100	600×2000
Д-9	Дверь скрытого монтажа	700×2100	600×2000
Д-10	Дверь скрытого монтажа	800×2100	700×2000
Д-11	Дверь скрытого монтажа	800×2100	700×2000
Д-12	Дверь скрытого монтажа	800×2100	700×2000
Д-13	Дверь скрытого монтажа	800×2100	700×2000

Примечания

1. Размеры — в мм от чистовых поверхностей стен до отделки; размеры уточнить по месту до начала работ.
2. Д-N, ПР-N в кружке — марка проёма: проём и полотно — по таблице проёмов, «расч.» полотно по проёму, заказ — по выбранной модели; ведомость, отделка и фурнитура — лист 45.
3. Несущие стены не изменять: проёмы, ниши и штробы в них — только по техническому заключению.
4. «расч.» — полотно, выведенное из проёма по запасу каталогов; заказ — по таблице проёмов выбранной модели; Д-7, Д-8, Д-9, Д-10, Д-11, Д-12, Д-13: проём 2100, а под полотно 2000 по каталогам нужен 2050–2080, под 2100 — 2150–2180: высоту проёма — по модели.

	Лист	№ док.	Подпись	Дата
Дизайнер	Кырлан А.С.			04.11.26


Проект: Дом 331 м² — **М 1:75**

План монтажный · Мансарда


Стадия	Лист	Листов
П	9	168

выпуск 04.11.2026 № f163a372b2 · стр. 9 из 168

Привязка выводов и крепление модулей

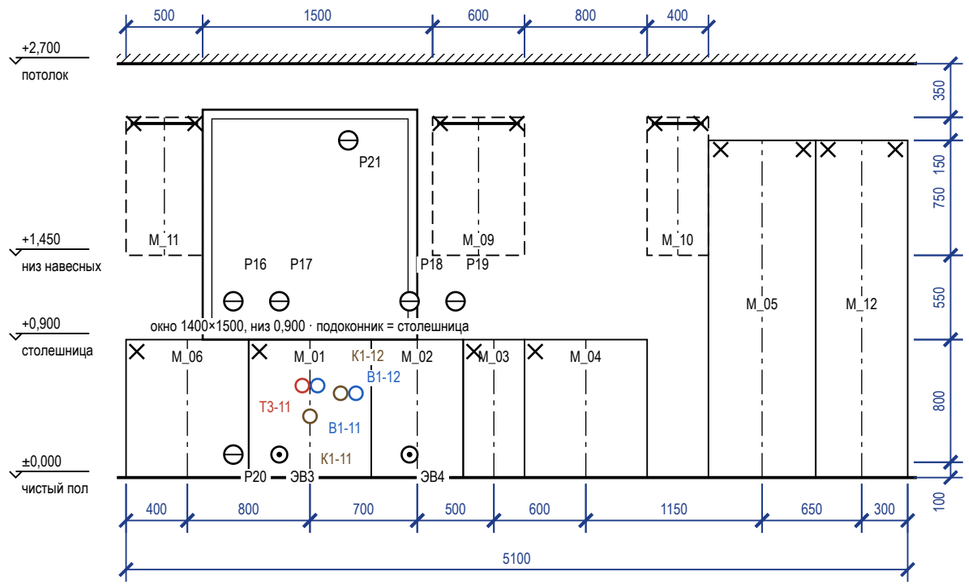

План столешницы

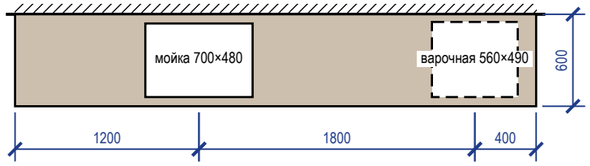

Примечания

1. Окно над M_06, M_01, M_02: низ проёма на 900 мм от пола, столешница на 900 мм, под окном мойка M_01 — смеситель упирается в створку, открывающуюся внутрь; примыкание столешницы к откосу и подоконнику — до решения: нужно решение заказчика (створка глухая или поворотно-откидная, поднять подоконник); столешницу у окна не раскраивать до решения.
2. Выводы — по проекту электрики и ВК; привязка по горизонтали — от оси модуля (плюс — вправо по виду), по высоте — от чистого пола до оси вывода.
3. Пенал — уголки к стене 2 шт. сверху; нижние модули — стяжками между собой и уголком к стене; ряд выставить по уровню опорами цоколя.
4. Розетки над столешницей — не ниже 150 мм над ней и не за корпусом техники; розетка за ПММ, духовым шкафом и холодильником — только в соседнем модуле или в зоне цоколя с доступом.
5. Столешница — вырезы по шаблонам выбранных моделей мойки и варочной панели; торцы у стены — герметик, пристеночный плинтус.

Привязка выводов к осям модулей

Код	Назначение	Модуль	От оси, мм	H, мм	Размещение
P16	розетка ×2 — фартук: мелкая техника	M_06	+300	1150	над столешницей (фартук)
P20	розетка — холодильник встроенный M_05 (розетка в соседнем модуле)	M_06	+300	150	в соседнем модуле, за ящиком
P17	розетка ×2 — фартук: мелкая техника	M_01	−200	1150	над столешницей (фартук)
ЭВ3	вывод кабеля — варочная панель M_04	M_01	−200	150	в модуле мойки
T3-11	T3 — межос. 100	M_01	−50	600	в модуле мойки
K1-11	K1 Ø50 — мойка	M_01	0	400	в модуле мойки
B1-11	B1 — межос. 100	M_01	+50	600	в модуле мойки
K1-12	K1 Ø40 — слив ПММ в шкафу мойки	M_01	+200	550	в модуле мойки
P21	розетка — вытяжка над варочной панелью M_04 (розетка за съёмной панелью)	M_01	+250	2200	над столешницей (фартук)
B1-12	B1 — кран ПММ в шкафу мойки	M_01	+300	550	в модуле мойки
P18	розетка ×2 — фартук: мелкая техника	M_02	−50	1150	над столешницей (фартук)
ЭВ4	вывод кабеля — духовой шкаф M_04 (вывод в соседнем модуле)	M_02	−50	150	за ПММ — перенести в соседний модуль
P19	розетка ×2 — фартук: мелкая техника	M_02	+250	1150	над столешницей (фартук)

Зазоры под отделку

Поверхность	Отделка	Зазор, мм	Учесть
фартук	керамогранит	10	от чернового основания до корпуса навесных и столешницы
стены	окраска	5	под штукатурку и шпаклёвку за пеналом
пол	инженерная доска		цоколь — после укладки пола, опоры ±20 мм


Условные обозначения

- нижний модуль, пенал (контур)
- невидимый контур: навесной модуль, корпус под столешницей
- ось модуля (от неё — привязка вывода)
- анкер / уголок крепления к стене
- розетка на стене
- вывод кабеля к технике
- B1 — вывод воды B1 / T3, канализации K1


					Проект: Дом 331 м² — **М 1:40**
	Лист	№ док.	Подпись	Дата	Кухня (пом. 1). Монтажная схема
Дизайнер	Кырлан А.С.			04.11.26	Стадия: П · Лист: 10 · Листов: 168

выпуск 04.11.2026 № f163a372b2 · стр. 10 из 168


Система хранения М_17 (пом. 4)

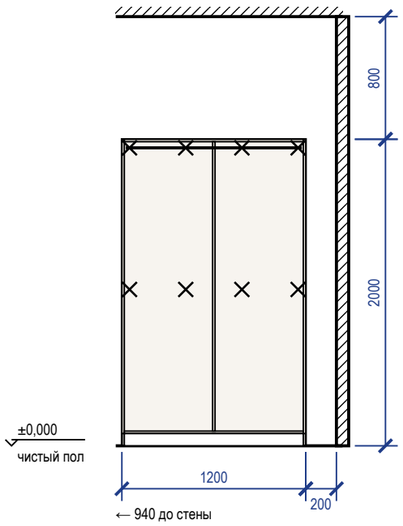


Система хранения М_23 (пом. 7)

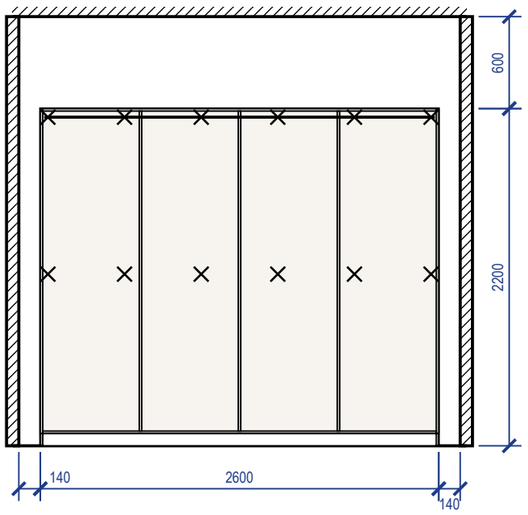

Шкаф-купе М_24 (пом. 8)

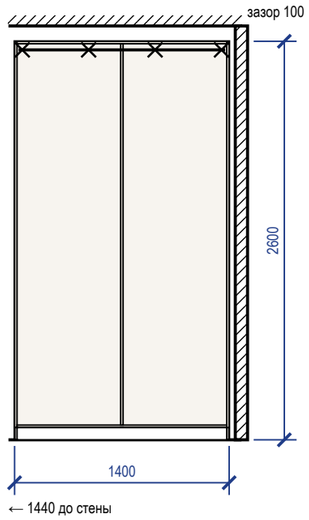

Система хранения М_26 (пом. 10)

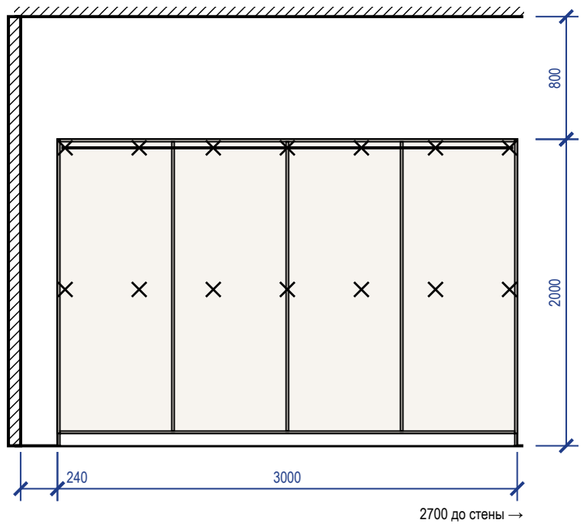

Крепление и зазоры под отделку (изделия листа 1)

Марка	Помещение, стена	Основание	Отделка стены	Зазор, мм	Крепёж по планке	От опрокидывания
М_17	Котельная (4), стена Г	по основанию — см. таблицу крепежа	окраска	5	анкер 8 шт. (2 ряда)	уголки 2 шт.
М_23	Кладовая (7), стена В	по основанию — см. таблицу крепежа	окраска	5	анкер 12 шт. (2 ряда)	уголки 2 шт.
М_24	Прихожая (8), стена А	по основанию — см. таблицу крепежа	окраска	5	анкер 4 шт., шаг 433	уголки 2 шт.
М_26	Гараж (10), стена А	по основанию — см. таблицу крепежа	окраска	5	анкер 14 шт. (2 ряда)	уголки 2 шт.

Крепёж по основанию стены

Основание стены	Крепёж
бетон, ж/б	анкер-шуруп 7,5×72 или дюбель 8×60 с шурупом 5×70
кирпич полнотелый	дюбель 8×80 с шурупом 5×90
газобетон, пазогребень	дюбель для газобетона 10×100 или химический анкер
гипсокартон	закладная до обшивки (брус 40×80 или фанера 18 мм), саморез в закладную

Условные обозначения


- анкер / уголок крепления к стене
- корпус и полки ЛДСП (вид на стену)
- компенсатор — короб до потолка

Примечания


1. Установочные размеры — от чистого пола и чистых стен; перед установкой контрольный замер после отделки.
2. Порядок: корпус выставить по уровню опорами цоколя → закрепить к стене по задней планке → навесить двери и фасады, отрегулировать зазоры → подогнать и закрепить компенсатор.
3. Анкеры — с шагом не более 500 мм, не ближе 50 мм от края планки; на ГКЛ только в закладную, установленную до обшивки.
4. Скрытые коммуникации под анкеры проверить детектором; трассы электрики по плану розеток.
5. Монтажная схема на 2 листах, лист 1 из 2; продолжение — на следующем листе схемы. Условные обозначения, таблица крепежа по основанию и примечания повторены на каждом листе.

					Проект: Дом 331 м²	М 1:40
	Лист	№ док.	Подпись	Дата		
Дизайнер	Кырлан А.С.			04.11.26	Шкафы. Монтажная схема. Лист 1 из 2	Стадия: П; Лист: 11; Листов: 168


Система хранения M_43 пом. 14

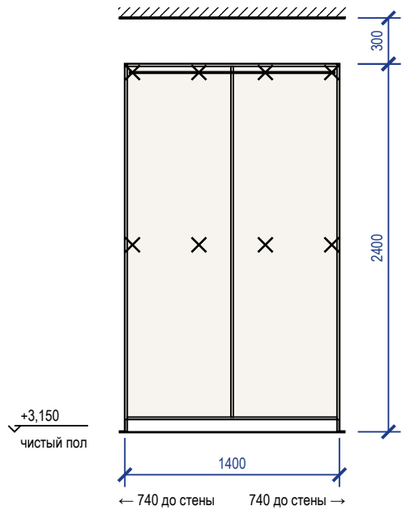


Шкаф распашной M_46 (пом. 16)

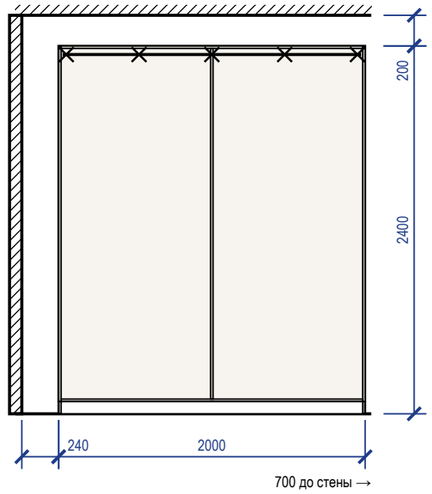


Система хранения M_49 (пом. 17)

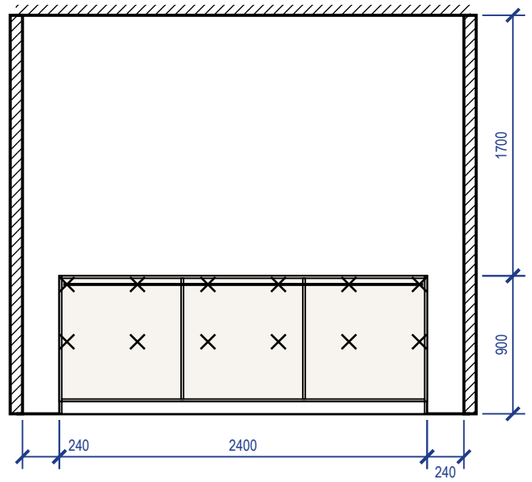

Шкаф распашной M_53 (пом. 18)

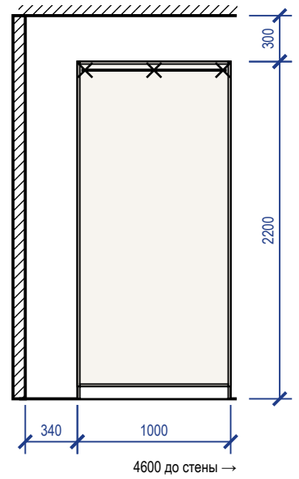

Шкаф распашной M_56 пом. 19

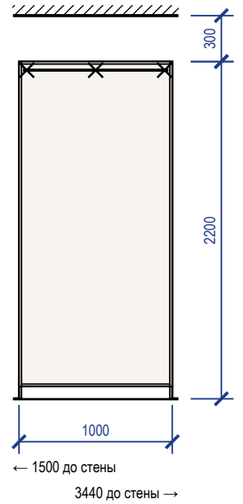

Крепление и зазоры под отделку (изделия листа 2)

Марка	Помещение, стена	Основание	Отделка стены	Зазор, мм	Крепёж по планке	От опрокидывания
M_43	Гардеробная мастер (14), стена B	по основанию — см. таблицу крепежа	окраска	5	анкер 8 шт. (2 ряда)	уголки 2 шт.
M_46	Спальня 2 (16), стена A	по основанию — см. таблицу крепежа	окраска	5	анкер 5 шт., шаг 475	уголки 2 шт.
M_49	Холл мансарды (17), стена B	по основанию — см. таблицу крепежа	окраска	5	анкер 12 шт. (2 ряда)	уголки 2 шт.
M_53	Спальня 3 (18), стена B	по основанию — см. таблицу крепежа	окраска	5	анкер 3 шт., шаг 450	уголки 2 шт.
M_56	Спальня 4 (19), стена A	по основанию — см. таблицу крепежа	окраска	5	анкер 3 шт., шаг 450	уголки 2 шт.

Крепёж по основанию стены

Основание стены	Крепёж
бетон, ж/б	анкер-шуруп 7,5×72 или дюбель 8×60 с шурупом 5×70
кирпич полнотелый	дюбель 8×80 с шурупом 5×90
газобетон, пазогребень	дюбель для газобетона 10×100 или химический анкер
гипсокартон	закладная до обшивки (брус 40×80 или фанера 18 мм), саморез в закладную

Условные обозначения


- анкер / уголок крепления к стене
- корпус и полки ЛДСП (вид на стену)
- компенсатор — короб до потолка

Примечания

1. Установочные размеры — от чистого пола и чистых стен; перед установкой контрольный замер после отделки.
2. Порядок: корпус выставить по уровню опорами цоколя → закрепить к стене по задней планке → навесить двери и фасады, отрегулировать зазоры → подогнать и закрепить компенсатор.
3. Анкеры — с шагом не более 500 мм, не ближе 50 мм от края планки; на ГКЛ только в закладную, установленную до обшивки.
4. Скрытые коммуникации под анкеры проверить детектором; трассы электрики по плану розеток.
5. Монтажная схема на 2 листах, лист 2 из 2. Условные обозначения, таблица крепежа по основанию и примечания повторены на каждом листе.

					Проект: Дом 331 м²	M 1:40
	Лист	№ док.	Подпись	Дата		
Дизайнер	Кырлан А.С.			04.11.26	Шкафы. Монтажная схема. Лист 2 из 2	Стадия: П; Лист: 12; Листов: 168

выпуск 04.11.2026 № f163a372b2 · стр. 12 из 168

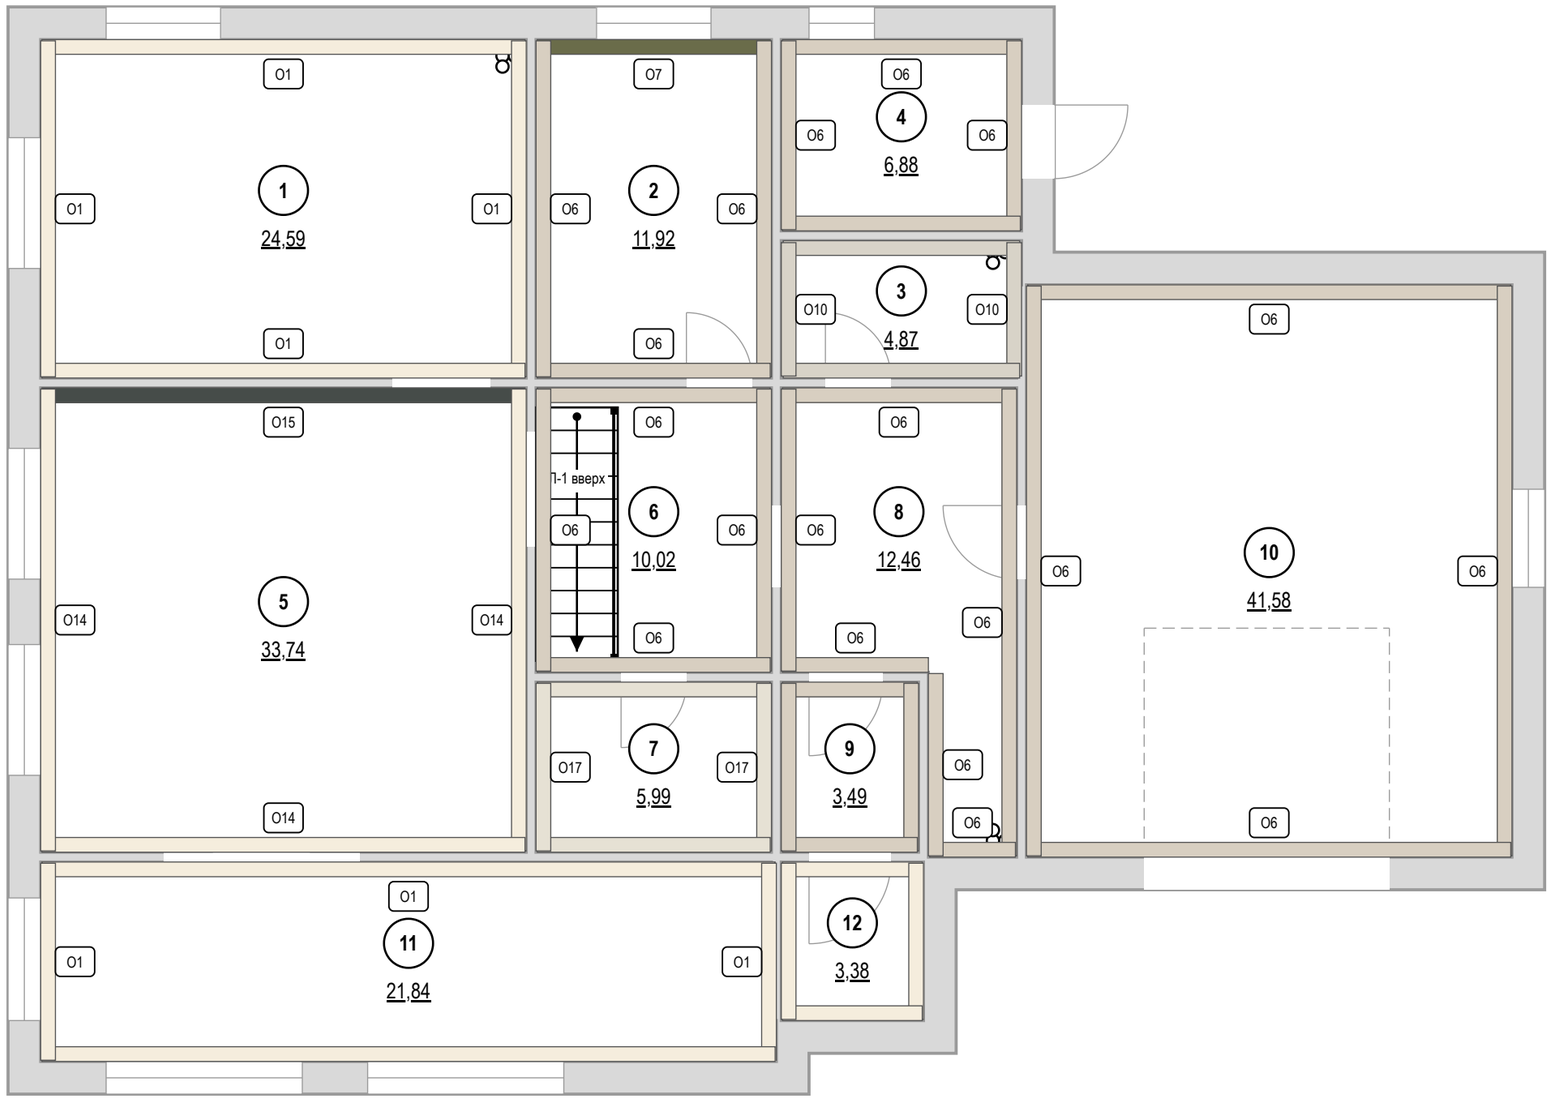


Покрытия стен

Марка	Покрытие	Помещение: S, м²	Итого, м²
О1	окраска Tikkurila · S 0804-Y30R «S 0804-Y30R»	1: 46,0; 11: 49,3; 12: 18,4	113,7
О6	окраска Farrow & Ball · No. 226 «Joa's White»	2: 28,2; 4: 26,6; 6: 25,6; 8: 38,5; 9: 16,7; 10: 62,3	198,0
О7	окраска Farrow & Ball · No. 298 «Bancha»	2: 5,9	5,9
О10	облицовка плиткой Atlas Concorde · A8UZ «Marvel Travertine» 600×1200 мм	3: 20,1	20,1
О14	окраска Tikkurila · S 0804-Y30R «S 0804-Y30R»	5: 32,6	32,6
О15	окраска Farrow & Ball · No. 93 «Studio Green — почти чёрный зелёный»	5: 12,8	12,8
О17	окраска Little Greene · No. 105 «Slaked Lime»	7: 25,8	25,8

Площади — нетто, по развёрткам (за вычетом проёмов и фартука); высоты помещений — от чистого пола.

					Проект: Дом 331 м² — М 1:75
	Лист	№ док.	Подпись	Дата	Карта покрытий стен · 1-й этаж
Дизайнер	Кырлан А.С.			04.11.26	Стадия: П; Лист: 13; Листов: 168

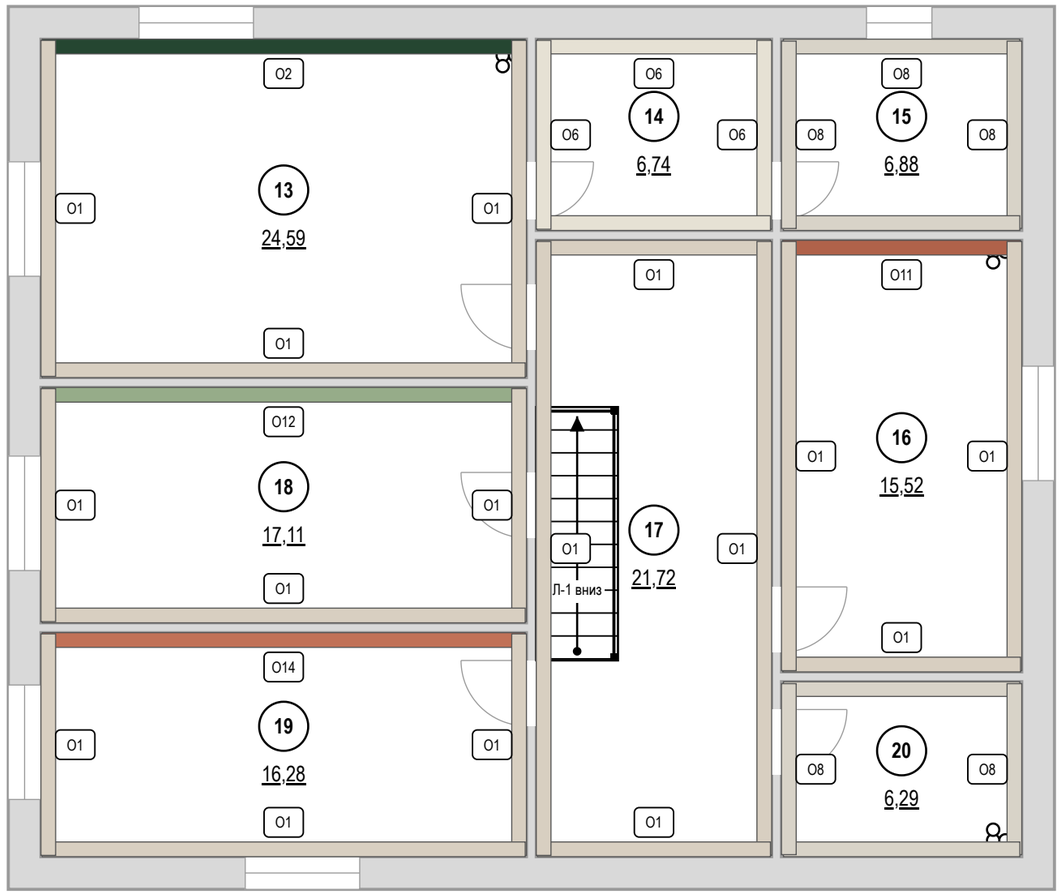

Покрытия стен

Марка	Покрытие	Помещение: S, м²	Итого, м²
О1	окраска Farrow & Ball · No. 226 «Joa's White»	13: 30,9; 16: 31,6; 17: 45,5; 18: 25,6; 19: 23,6	157,1
О2	окраска Tikkurila · S 7020-G10Y «Хвойный тёмно-зелёный»	13: 13,3	13,3
О6	окраска Little Greene · No. 105 «Slaked Lime»	14: 24,9	24,9
О8	облицовка плиткой Atlas Concorde · A8UZ «Marvel Travertine» 600×1200 мм	15: 22,8; 20: 22,3	45,1
О11	окраска Farrow & Ball · No. 64 «Red Earth»	16: 7,6	7,6
О12	окраска Tikkurila · S 3020-G30Y «S 3020-G30Y»	18: 14,8	14,8
О14	окраска Tikkurila · S 3040-Y70R «S 3040-Y70R»	19: 14,8	14,8

Площади — нетто, по развёрткам (за вычетом проёмов и фартука); высоты помещений — от чистого пола.

					Проект: Дом 331 м² — М 1:75
	Лист	№ док.	Подпись	Дата	
Дизайнер	Кырлан А.С.			04.11.26	Карта покрытий стен · Мансарда

Стадия	Лист	Листов
П	14	168

выпуск 04.11.2026 № f163a372b2 · стр. 14 из 168

Колерная карта по помещениям

Помещение	Поверхность	Образец	Поз.	Система и код цвета	Производитель, линейка / материал, артикул	Блеск	Класс истирания	LRV	Площадь
1. Кухня-столовая 24,59 м²	стены		**К1**	NCS S 0804-Y30R	Tikkurila · Luja 7	полуматов.	1	85	44,8 м²
	потолок		**К2**	NCS S 0804-Y30R	Tikkurila · Luja 7	матовая	1	85	24,6 м²
	пол		**КМ1**	по образцу	Coswick · Вековые традиции · арт. 1167-4250				24,6 м²
	плинтус		**К3**	NCS S 0804-Y30R	МДФ · в цвет NCS	полуглянц.	2	85	18,3 м
	фартук		**КМ2**	тон Paper F497 (тёплый белый)	керамогранит · аналог по хар.				1,1 м²
2. Кабинет-гостевая 11,92 м²	стены		**К4**	Farrow & Ball No. 226	Farrow & Ball · Modern Emulsion	матовая	1	63	25,3 м²
	акцент А		**К5**	Farrow & Ball No. 298	Farrow & Ball · Modern Emulsion	матовая	1	14	5,7 м²
	потолок		**К6**	Little Greene No. 105	Little Greene · Absolute Matt	глубокомат.	2	82	11,9 м²
	пол		**КМ1**	по образцу	Coswick · Вековые традиции · арт. 1167-4250				11,9 м²
	плинтус		**К7**	Farrow & Ball No. 226	МДФ · в цвет Farrow & Ball			63	11,7 м
3. Санузел 1 этажа 4,87 м²	стены		**КМ3**	Marvel Travertine	Atlas Concorde · арт. A8UZ				20,5 м²
	потолок		**К8**	Little Greene No. 105	Little Greene · Intelligent Bathroom	матовая	1	82	4,9 м²
	пол		**КМ4**	по образцу	керамогранит · аналог по хар.				4,9 м²
4. Котельная 6,88 м²	стены		**К4**	Farrow & Ball No. 226	Farrow & Ball · Modern Emulsion	матовая	1	63	27,0 м²
	потолок		**К6**	Little Greene No. 105	Little Greene · Absolute Matt	глубокомат.	2	82	6,9 м²
	пол		**КМ5**	Marvel Travertine	Atlas Concorde · арт. A8UZ				6,9 м²
	плинтус		**К7**	Farrow & Ball No. 226	МДФ · в цвет Farrow & Ball			63	9,7 м
5. Гостиная 33,74 м²	стены		**К9**	NCS S 0804-Y30R	Tikkurila · Optiva 5 Matt	матовая	2	85	32,2 м²
	акцент А		**К10**	Farrow & Ball No. 93	Farrow & Ball · Modern Emulsion	матовая	1	7	12,9 м²
	потолок		**К11**	NCS S 0804-Y30R	Tikkurila · Anti-Reflex 2	глубокомат.	2	85	33,7 м²
	пол		**КМ1**	по образцу	Coswick · Вековые традиции · арт. 1167-4250				33,7 м²
	плинтус		**К3**	NCS S 0804-Y30R	МДФ · в цвет NCS	полуглянц.	2	85	18,2 м
6. Холл с лестницей 10,02 м²	стены		**К4**	Farrow & Ball No. 226	Farrow & Ball · Modern Emulsion	матовая	1	63	22,3 м²
	потолок		**К6**	Little Greene No. 105	Little Greene · Absolute Matt	глубокомат.	2	82	10,0 м²
	пол		**КМ1**	по образцу	Coswick · Вековые традиции · арт. 1167-4250				10,0 м²
	плинтус		**К7**	Farrow & Ball No. 226	МДФ · в цвет Farrow & Ball			63	7,0 м
7. Кладовая 5,99 м²	стены		**К12**	Little Greene No. 105	Little Greene · Intelligent Matt	матовая	1	82	23,3 м²
	потолок		**К6**	Little Greene No. 105	Little Greene · Absolute Matt	глубокомат.	2	82	6,0 м²
	пол		**КМ1**	по образцу	Coswick · Вековые традиции · арт. 1167-4250				6,0 м²
	плинтус		**К13**	Little Greene No. 105	МДФ · в цвет Little Greene			82	7,8 м
8. Прихожая 12,46 м²	стены		**К4**	Farrow & Ball No. 226	Farrow & Ball · Modern Emulsion	матовая	1	63	39,0 м²
	потолок		**К6**	Little Greene No. 105	Little Greene · Absolute Matt	глубокомат.	2	82	12,5 м²
	пол		**КМ5**	Marvel Travertine	Atlas Concorde · арт. A8UZ				12,5 м²
	плинтус		**К7**	Farrow & Ball No. 226	МДФ · в цвет Farrow & Ball			63	13,6 м
9. Тамбур 3,49 м²	стены		**К4**	Farrow & Ball No. 226	Farrow & Ball · Modern Emulsion	матовая	1	63	17,1 м²
	потолок		**К6**	Little Greene No. 105	Little Greene · Absolute Matt	глубокомат.	2	82	3,5 м²
	пол		**КМ5**	Marvel Travertine	Atlas Concorde · арт. A8UZ				3,5 м²
	плинтус		**К7**	Farrow & Ball No. 226	МДФ · в цвет Farrow & Ball			63	5,6 м
10. Гараж 41,58 м²	стены		**К4**	Farrow & Ball No. 226	Farrow & Ball · Modern Emulsion	матовая	1	63	62,6 м²
	потолок		**К6**	Little Greene No. 105	Little Greene · Absolute Matt	глубокомат.	2	82	41,6 м²
	пол		**КМ6**	по образцу	аналог по хар.				41,6 м²
	плинтус		**КМ7**	по образцу	ПВХ · аналог по хар.				22,0 м

Примечания

1. Цвет на листе и на экране — ориентир. До покраски — выкрас на объекте: не меньше А3 (или лист ГКЛ), на грунте под эту краску, не на белой шпаклёвке, в 2 слоя; на обороте — код, бренд, веер, дата. Смотреть днём и вечером, рядом с образцами пола и плитки. Красить только в цвет утверждённого выкраса.
2. Краску заказывать по коду из графы «Система и код цвета» у бренда этого кода, не «аналогом» другого; весь объём одного кода — одной партией, колеруемую краску — за один проход машины.
3. Площади — те же, что в ведомости отделки (лист С1); сколько краски заказать — в спецификации отделочных материалов (лист С5).
4. Колерная карта на 2 листах: обозначения — на каждом (на этом — позиции его помещений), схема и палитра — на первом, выкрасы — на последнем.

Схема палитры проекта

Стиль: Шале 60% + Эко и органический модерн 40% · схема: комплементарная

основной Farrow & Ball No. 226	основной NCS S 0804-Y30R	основной Little Greene No. 105	второстепенный Tikkurila V451	второстепенный NCS S 3020-G30Y	второстепенный Tikkurila X463	второстепенный Farrow & Ball No. 229	второстепенный Farrow & Ball No. 40	второстепенный Farrow & Ball No. 245	второстепенный NCS S 2005-Y20R	второстепенный NCS S 3010-Y30R	акцентный NCS S 7020-G10Y	акцентный Farrow & Ball No. 04	акцентный Farrow & Ball No. 43
Joa's White LRV 63 стены 2,4,6,8,9,10,13,16,17,18,19; плинтус 1,4,6,8,9,10,11,12,15,16 · высота плинтуса 2,5	тёплый молочный белый LRV 85 стены 1,5,11,12; потолок 1,5,11,12 · плинтус 1,5,11,12 · высота плинтуса 2,5	Slaked Lime LRV 82 потолок 2,3,4,5,7,8,9,11,12,14,15,16,17,18,19,20 стены 7,14 · плинтус 7,14 · высота плинтуса 12,5	Olive grove V451 LRV 51 текстиль/декор 18	шалфей LRV 38 акцент 18; текстиль/декор 17,18	Sandstone X463 LRV 51 текстиль/декор 2,16,19	Elephant's Ear LRV 52 текстиль/декор 13	Mouse's Ear LRV 26 текстиль/декор 2	Charleston Grey LRV 30 текстиль/декор 5,10	Светлый песочно-серый LRV 60 текстиль/декор 1,5,13,18,19	орех/лён тёмный LRV 43 текстиль/декор 2,16,19	Хвойный тёмно-зелёный LRV ≈5 акцент 13; текстиль/декор 13	Red Earth LRV 18 акцент 16; текстиль/декор 16	Eating Room Red – брусничный серый LRV 11.8 в отделке не применён

План 60/30/10

Окраска, факт — по площади стен, акцентов, потолков

окрашено всего 881,3 м²; серым — цвета вне палитры; второстепенный тон несут мебель и текстиль

Условные обозначения

- **К1** NCS S 0804-Y30R · тёплый молочный белый · Tikkurila Luja 7 · полуматов. · кл. 1
- **К2** NCS S 0804-Y30R · тёплый молочный белый · Tikkurila Luja 7 · матовая · кл. 1
- **К3** NCS S 0804-Y30R · тёплый молочный белый · МДФ · полуглянц. · кл. 2
- **К4** Farrow & Ball No. 226 · Joa's White · Modern Emulsion · матовая · кл. 1
- **К5** Farrow & Ball No. 298 · Bancha · Modern Emulsion · матовая · кл. 1
- **К6** Little Greene No. 105 · Slaked Lime · Absolute Matt · глубокомат. · кл. 2
- **К7** Farrow & Ball No. 226 · Joa's White · МДФ
- **К8** Little Greene No. 105 · Slaked Lime · Intelligent Bathroom · матовая · кл. 1
- **К9** NCS S 0804-Y30R · тёплый молочный белый · Tikkurila Optiva 5 Matt · матовая · кл. 2
- **К10** Farrow & Ball No. 93 · Studio Green — почти чёрный зелёный · Modern Emulsion · матовая · кл. 1
- дерево (доска, паркет, ламинат) — рисунок досок
- керамогранит, плитка, камень — сетка швов по формату
- материал без кода цвета — по образцу (артикул в ведомости отделки)

- **К11** NCS S 0804-Y30R · тёплый молочный белый · Tikkurila Anti-Reflex 2 · глубокомат. · кл. 2
- **К12** Little Greene No. 105 · Slaked Lime · Intelligent Matt · матовая · кл. 1
- **К13** Little Greene No. 105 · Slaked Lime · МДФ
- **КМ1** инженерная доска · 1167-4250
- **КМ2** аналог: керамогранит матовый, тон F497, 600×600×9 мм
- **КМ3** плитка · A8UZ
- **КМ4** аналог: керамогранит ректифицированный под травертин, матовый, 600×600×9 мм
- **КМ5** керамогранит · A8UZ
- **КМ6** аналог: наливной полимерный пол (эпоксидный), с кварцевой посыпкой, 3 мм
- **КМ7** ПВХ · аналог: плинтус ПВХ влагостойкий 100 мм, серый

К — краска, КМ — отделочный материал (тон КМ — по описанию, эталон — образец материала); кл. — класс истирания (1 — самый стойкий к мытью); LRV — светлота цвета: 0 — чёрный, 100 — белый

					Проект: Дом 331 м²		
	Лист	№ док.	Подпись	Дата	Колерная карта	Стадия	Лист	Листов
Дизайнер	Кырлан А.С.			04.11.26		П	15	168

Колерная карта по помещениям (продолжение)

Помещение	Поверхность	Образец	Поз.	Система и код цвета	Производитель, линейка / материал, артикул	Блеск	Класс истирания	LRV	Площадь
11. Веранда 21,84 м²	стены		**K1**	NCS S 0804-Y30R	Tikkurila · Luja 7	полуматов.	1	85	49,6 м²
	потолок		**K2**	NCS S 0804-Y30R	Tikkurila · Luja 7	матовая	1	85	21,8 м²
	пол		**KM5**	тон Claystone V486 (грейж)	Atlas Concorde · Marvel Travertine · арт. A8UZ				21,8 м²
	плинтус		**KM8**	тон Claystone V486 (грейж)	керамогранит · аналог по хар.				20,5 м
12. Крыльцо 3,38 м²	стены		**K1**	NCS S 0804-Y30R	Tikkurila · Luja 7	полуматов.	1	85	18,7 м²
	потолок		**K2**	NCS S 0804-Y30R	Tikkurila · Luja 7	матовая	1	85	3,4 м²
	пол		**KM5**	тон Claystone V486 (грейж)	Atlas Concorde · Marvel Travertine · арт. A8UZ				3,4 м²
	плинтус		**KM8**	тон Claystone V486 (грейж)	керамогранит · аналог по хар.				6,4 м
13. Спальня мастер 24,59 м²	стены		**K4**	Farrow & Ball No. 226	Farrow & Ball · Modern Emulsion	матовая	1	63	28,6 м²
	акцент A		**K14**	NCS S 7020-G10Y	Tikkurila · Optiva 5 Matt	матовая	2	≈5	7,6 м²
	потолок		**K6**	Little Greene No. 105	Little Greene · Absolute Matt	глубокомат.	2	82	27,1 м²
	пол		**KM1**	по образцу	Coswick · Вековые традиции · арт. 1167-4250				24,6 м²
	плинтус		**K7**	Farrow & Ball No. 226	МДФ · в цвет Farrow & Ball			63	18,7 м
14. Гардеробная мастер 6,74 м²	стены		**K12**	Little Greene No. 105	Little Greene · Intelligent Matt	матовая	1	82	18,7 м²
	потолок		**K6**	Little Greene No. 105	Little Greene · Absolute Matt	глубокомат.	2	82	8,6 м²
	пол		**KM1**	по образцу	Coswick · Вековые традиции · арт. 1167-4250				6,7 м²
	плинтус		**K13**	Little Greene No. 105	МДФ · в цвет Little Greene			82	9,0 м
15. Санузел мастер 6,88 м²	стены		**KM3**	Marvel Travertine	Atlas Concorde · арт. A8UZ				19,9 м²
	потолок		**K8**	Little Greene No. 105	Little Greene · Intelligent Bathroom	матовая	1	82	7,8 м²
	пол		**KM4**	по образцу	керамогранит · аналог по хар.				6,9 м²
16. Спальня 2 15,52 м²	стены		**K4**	Farrow & Ball No. 226	Farrow & Ball · Modern Emulsion	матовая	1	63	28,1 м²
	акцент A		**K15**	Farrow & Ball No. 64	Farrow & Ball · Modern Emulsion	матовая	1	18	7,3 м²
	потолок		**K6**	Little Greene No. 105	Little Greene · Absolute Matt	глубокомат.	2	82	15,5 м²
	пол		**KM1**	по образцу	Coswick · Вековые традиции · арт. 1167-4250				15,5 м²
	плинтус		**K7**	Farrow & Ball No. 226	МДФ · в цвет Farrow & Ball			63	14,7 м
17. Холл мансарды 21,72 м²	стены		**K4**	Farrow & Ball No. 226	Farrow & Ball · Modern Emulsion	матовая	1	63	34,8 м²
	потолок		**K6**	Little Greene No. 105	Little Greene · Absolute Matt	глубокомат.	2	82	23,5 м²
	пол		**KM1**	по образцу	Coswick · Вековые традиции · арт. 1167-4250				21,7 м²
	плинтус		**K7**	Farrow & Ball No. 226	МДФ · в цвет Farrow & Ball			63	14,4 м
18. Спальня 3 17,11 м²	стены		**K4**	Farrow & Ball No. 226	Farrow & Ball · Modern Emulsion	матовая	1	63	25,5 м²
	акцент A		**K16**	NCS S 3020-G30Y	Tikkurila · Optiva 5 Matt	матовая	2	38	12,3 м²
	потолок		**K6**	Little Greene No. 105	Little Greene · Absolute Matt	глубокомат.	2	82	17,1 м²
	пол		**KM1**	по образцу	Coswick · Вековые традиции · арт. 1167-4250				17,1 м²
	плинтус		**K17**	Farrow & Ball No. 226	Orac Decor · Contour (Luxxus)			63	15,6 м
19. Спальня 4 16,28 м²	стены		**K4**	Farrow & Ball No. 226	Farrow & Ball · Modern Emulsion	матовая	1	63	15,8 м²
	акцент A		**K18**	NCS S 3040-Y70R	Tikkurila · Optiva 5 Matt	матовая	2	24	14,8 м²
	потолок		**K6**	Little Greene No. 105	Little Greene · Absolute Matt	глубокомат.	2	82	18,8 м²
	пол		**KM1**	по образцу	Coswick · Вековые традиции · арт. 1167-4250				16,3 м²
	плинтус		**K17**	Farrow & Ball No. 226	Orac Decor · Contour (Luxxus)			63	16,6 м
20. Санузел 2 6,29 м²	стены		**KM3**	Marvel Travertine	Atlas Concorde · арт. A8UZ				17,8 м²
	потолок		**K8**	Little Greene No. 105	Little Greene · Intelligent Bathroom	матовая	1	82	8,2 м²
	пол		**KM4**	по образцу	керамогранит · аналог по хар.				6,3 м²

Примечания

1. Цвет на листе и на экране — ориентир. До покраски — выкрас на объекте: не меньше А3 (или лист ГКЛ), на грунте под эту краску, не на белой шпаклёвке, в 2 слоя; на обороте — код, бренд, веер, дата. Смотреть днём и вечером, рядом с образцами пола и плитки; к основному цвету стен — ещё 2 соседних оттенка. Красить только в цвет утверждённого выкраса.
2. Краску заказывать по коду из графы «Система и код цвета» у бренда этого кода, не «аналогом» другого; весь объём одного кода — одной партией, колеруемую краску — за один проход машины.
3. Площади — те же, что в ведомости отделки (лист С1); сколько краски заказать — в спецификации отделочных материалов (лист С5).
4. Колерная карта на 2 листах: обозначения — на каждом, схема и палитра — на первом, выкрасы — на последнем.

Условные обозначения

- **K1** NCS S 0804-Y30R · тёплый молочный белый · Tikkurila Luja 7 · полуматов. · кл. 1
- **K2** NCS S 0804-Y30R · тёплый молочный белый · Tikkurila Luja 7 · матовая · кл. 1
- **K3** NCS S 0804-Y30R · тёплый молочный белый · МДФ · полуглянц. · кл. 2
- **K4** Farrow & Ball No. 226 · Joa's White · Modern Emulsion · матовая · кл. 1
- **K5** Farrow & Ball No. 298 · Bancha · Modern Emulsion · матовая · кл. 1
- **K6** Little Greene No. 105 · Slaked Lime · Absolute Matt · глубокомат. · кл. 2
- **K7** Farrow & Ball No. 226 · Joa's White · МДФ
- **K8** Little Greene No. 105 · Slaked Lime · Intelligent Bathroom · матовая · кл. 1
- **K9** NCS S 0804-Y30R · тёплый молочный белый · Tikkurila Optiva 5 Matt · матовая · кл. 2
- **K10** Farrow & Ball No. 93 · Studio Green — почти чёрный зелёный · Modern Emulsion · матовая · кл. 1
- **K11** NCS S 0804-Y30R · тёплый молочный белый · Tikkurila Anti-Reflex 2 · глубокомат. · кл. 2
- **K12** Little Greene No. 105 · Slaked Lime · Intelligent Matt · матовая · кл. 1
- **K13** Little Greene No. 105 · Slaked Lime · МДФ
- **K14** NCS S 7020-G10Y · Хвойный тёмно-зелёный · Tikkurila Optiva 5 Matt · матовая · кл. 2
- **K15** Farrow & Ball No. 64 · Red Earth · Modern Emulsion · матовая · кл. 1
- **K16** NCS S 3020-G30Y · шалфей · Tikkurila Optiva 5 Matt · матовая · кл. 2
- **K17** Farrow & Ball No. 226 · Joa's White · Contour (Luxxus)
- **K18** NCS S 3040-Y70R · обожжённая глина · Tikkurila Optiva 5 Matt · матовая · кл. 2
- **KM1** инженерная доска · 1167-4250
- **KM2** аналог: керамогранит матовый, тон F497, 600×600×9 мм
- **KM3** плитка · A8UZ
- **KM4** аналог: керамогранит ректифицированный под травертин, матовый, 600×600×9 мм
- **KM5** керамогранит · A8UZ
- **KM6** аналог: наливной полимерный пол (эпоксидный), с кварцевой посыпкой, 3 мм
- **KM7** ПВХ · аналог: плинтус ПВХ влагостойкий 100 мм, серый
- **KM8** керамогранит · аналог: плинтус из керамогранита пола, подрезка 80 мм, верхняя кромка с запилом 45°

дерево (доска, паркет, ламинат) — рисунок досок

керамогранит, плитка, камень — сетка швов по формату

материал без кода цвета — по образцу (артикул в ведомости отделки)

К — краска, КМ — отделочный материал (тон КМ — по описанию, эталон — образец материала); кл. — класс истирания (1 — самый стойкий к мытью); LRV — светлота цвета: 0 — чёрный, 100 — белый; «≈» — ориентировочно


Перечень выкрасов на согласование

№	Код	Бренд / веер	Пом. / стена	Подложка	Формат	Статус
1	S 0804-Y30R	NCS Tikkurila	1, 5, 11, 12	ГКЛ с грунтом; МДФ под эмаль	600×1000; 300×600	к выполнению
2	No. 226	Farrow & Ball	2, 4, 6, 8, 9, 10, 13, 16, 17, 18, 19	ГКЛ с грунтом; МДФ под эмаль	600×1000; 300×600	к выполнению
3	No. 298	Farrow & Ball	2 A	ГКЛ с грунтом	600×1000	к выполнению
4	No. 105	Little Greene	2, 3, 4, 6, 7, 8, 9, 10, 13, 14, 15, 16, 17, 18, 19, 20	ГКЛ с грунтом; МДФ под эмаль	600×1000; 300×600	к выполнению
5	No. 93	Farrow & Ball	5 A	ГКЛ с грунтом	600×1000	к выполнению
6	S 7020-G10Y	NCS Tikkurila	13 A	ГКЛ с грунтом	600×1000	к выполнению
7	No. 64	Farrow & Ball	16 A	ГКЛ с грунтом	600×1000	к выполнению
8	S 3020-G30Y	NCS Tikkurila	18 A	ГКЛ с грунтом	600×1000	к выполнению
9	S 3040-Y70R	NCS Tikkurila	19 A	ГКЛ с грунтом	600×1000	к выполнению

					Проект: Дом 331 м²
	Лист	№ док.	Подпись	Дата	
Дизайнер	Кырлан А.С.			04.11.26	Колерная карта

Стадия	Лист	Листов
П	16	168

выпуск 04.11.2026 № f163a372b2 · стр. 16 из 168

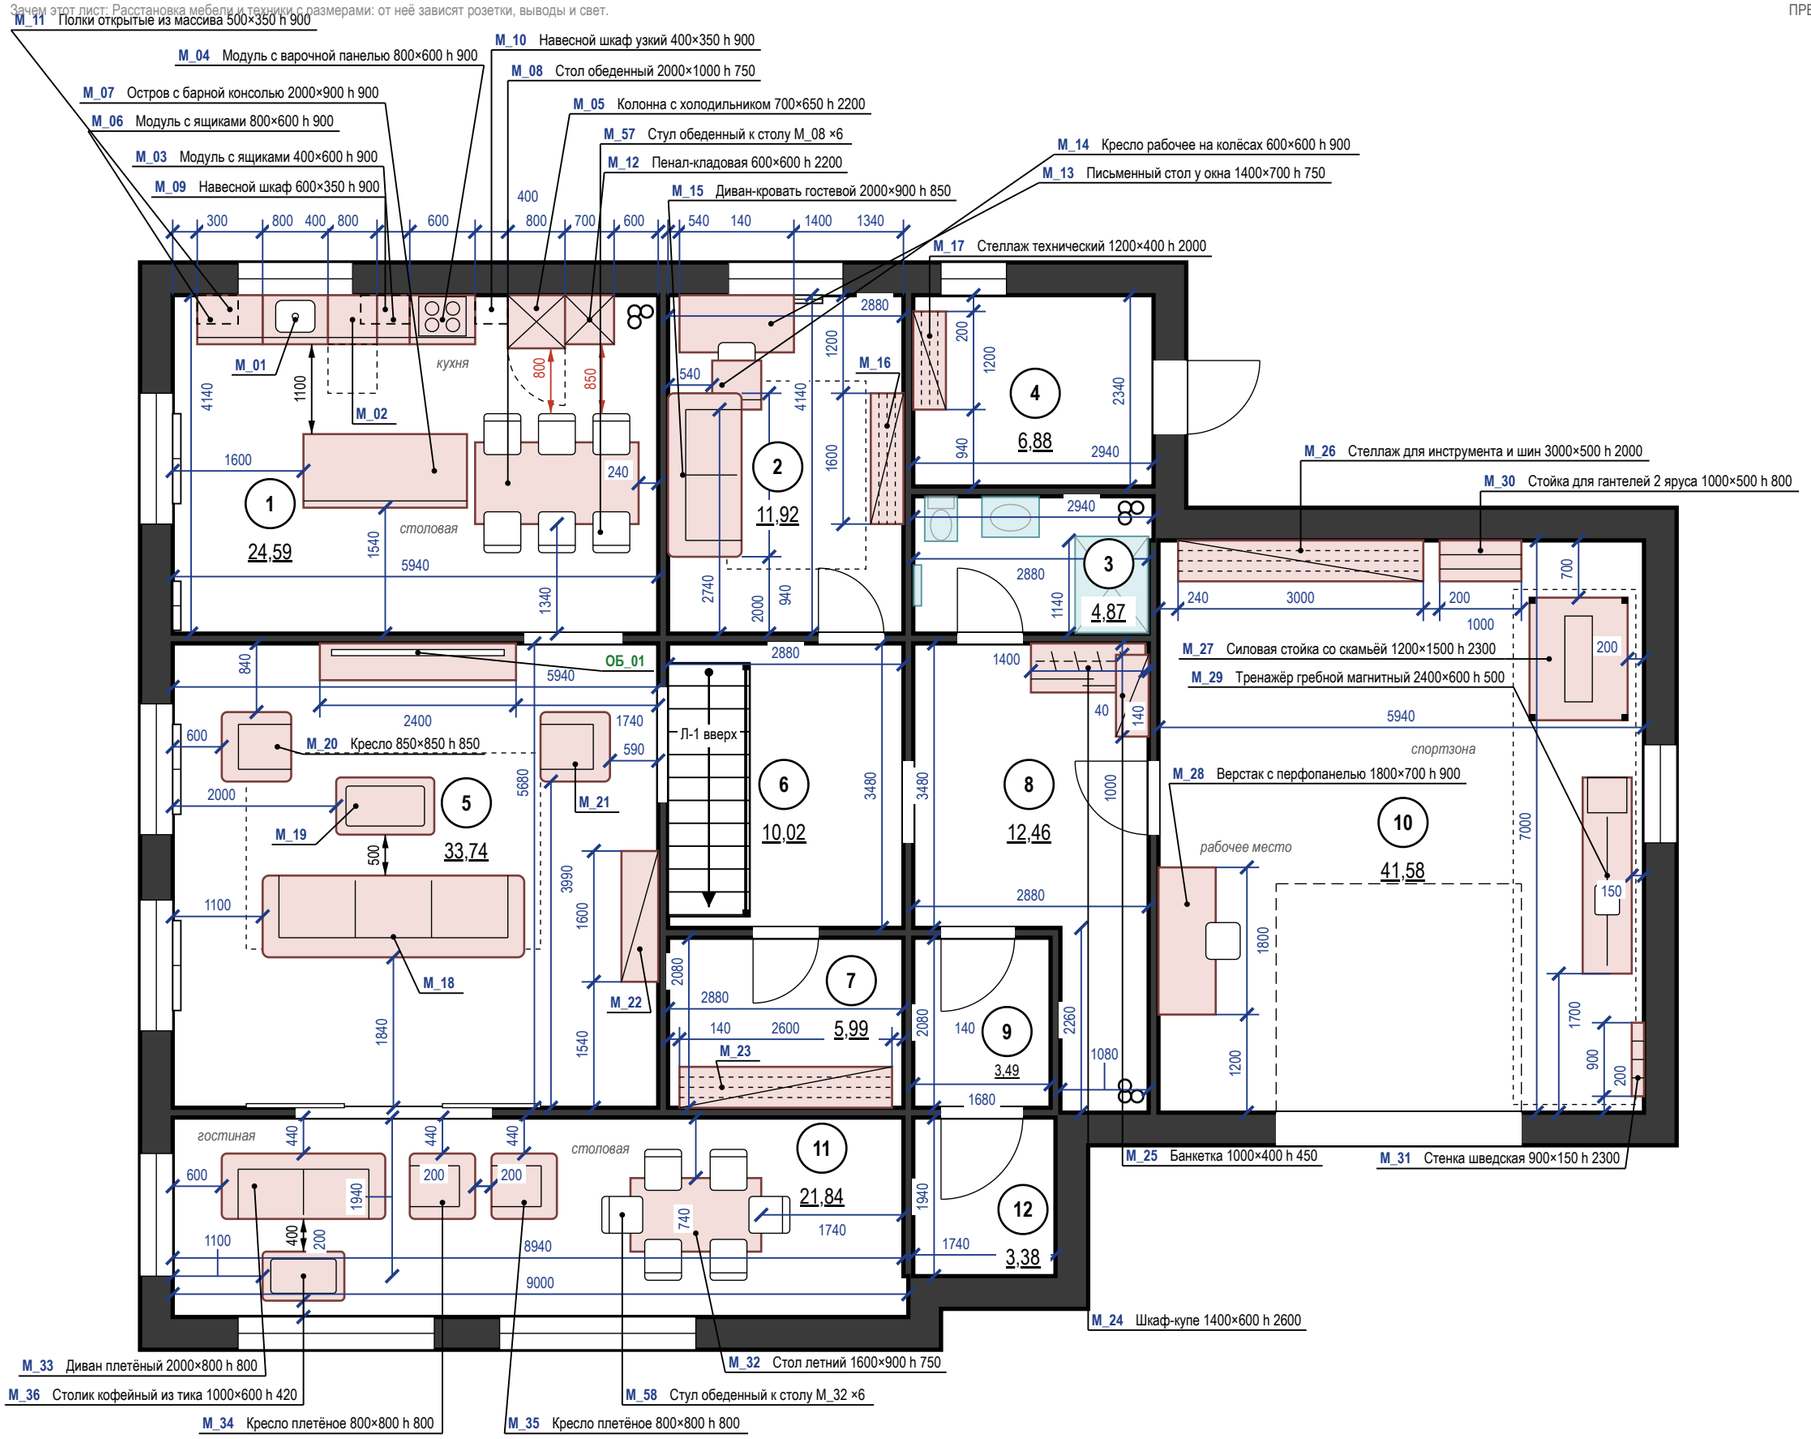

Экспликация помещений

лист 6 · на плане — номера в марках

Ведомость мебели и оборудования

Марка	Наименование	Ш×Г×В, мм	Пом.	Кол.
M_01	Модуль под мойку у окна	800×600×900	1	1
M_02	Посудомоечная машина встроенная	600×600×900	1	1
M_03	Модуль с ящиками	400×600×900	1	1
M_04	Модуль с варочной панелью	800×600×900	1	1
M_05	Колонна с холодильником	700×650×2200	1	1
M_06	Модуль с ящиками	800×600×900	1	1
M_07	Остров с барной консолью	2000×900×900	1	1
M_08	Стол обеденный 2000×1000	2000×1000×750	1	1
M_09	Навесной шкаф	600×350×900	1	1
M_10	Навесной шкаф узкий	400×350×900	1	1
M_11	Полки открытые из массива	500×350×900	1	1
M_12	Пенал-кладовая	600×600×2200	1	1
M_13	Письменный стол у окна	1400×700×750	2	1
M_14	Кресло рабочее на колёсах	600×600×900	2	1
M_15	Диван-кровать гостевой	2000×900×850	2	1
M_16	Стеллаж для книг	1600×400×2200	2	1
M_17	Стеллаж технический	1200×400×2000	4	1
ОБ_01	ТВ-стена с камином	2400×450×600	5	1
M_18	Диван угловой	3200×1000×820	5	1
M_19	Столик журнальный	1200×700×420	5	1
M_20	Кресло	850×850×850	5	1
M_21	Кресло-качалка	850×850×850	5	1
M_22	Буфет низкий	1600×450×800	5	1
M_23	Стеллаж для хранения	2600×500×2200	7	1
M_24	Шкаф-купе	1400×600×2600	8	1
M_25	Банкетка	1000×400×450	8	1
M_26	Стеллаж для инструмента и шин	3000×500×2000	10	1
M_27	Силовая стойка со скамьёй	1200×1500×2300	10	1
M_28	Верстак с перфопанелью	1800×700×900	10	1
M_29	Тренажёр гребной магнитный	2400×600×500	10	1
M_30	Стойка для гантелей 2 яруса	1000×500×800	10	1
M_31	Стенка шведская	900×150×2300	10	1
M_32	Стол летний	1600×900×750	11	1
M_33	Диван плетёный	2000×800×800	11	1
M_34	Кресло плетёное	800×800×800	11	1
M_35	Кресло плетёное	800×800×800	11	1
M_36	Столик кофейный из тика	1000×600×420	11	1
M_57	Стул обеденный к столу M_08	450×500×820	1	6
M_58	Стул обеденный к столу M_32	450×500×820	11	6

Ш — вдоль стены (изголовья), Г — от стены (длина кровати)

Материалы, модели, допуск замены — лист 19

Примечания


1. Размеры — в мм от чистовых поверхностей стен; размеры мебели уточнить после отделочных работ; общие указания — лист 3.
2. У позиций M_01, M_02, M_16, ОБ_01, M_18, M_19, M_21, M_22, M_23 на плане только марка: наименование и габарит — в спецификации, лист 19.
3. Стулья обеденной группы (M_57 — 6 шт., M_58 — 6 шт.) показаны в рабочем положении, задвинутыми под столешницу на 150 мм.

	Лист	№ док.	Подпись	Дата
Дизайнер	Кырлан А.С.			04.11.26

Проект: Дом 331 м² — **М 1:75**

План размещения мебели и оборудования · 1-й этаж

Стадия	Лист	Листов
П	17	168

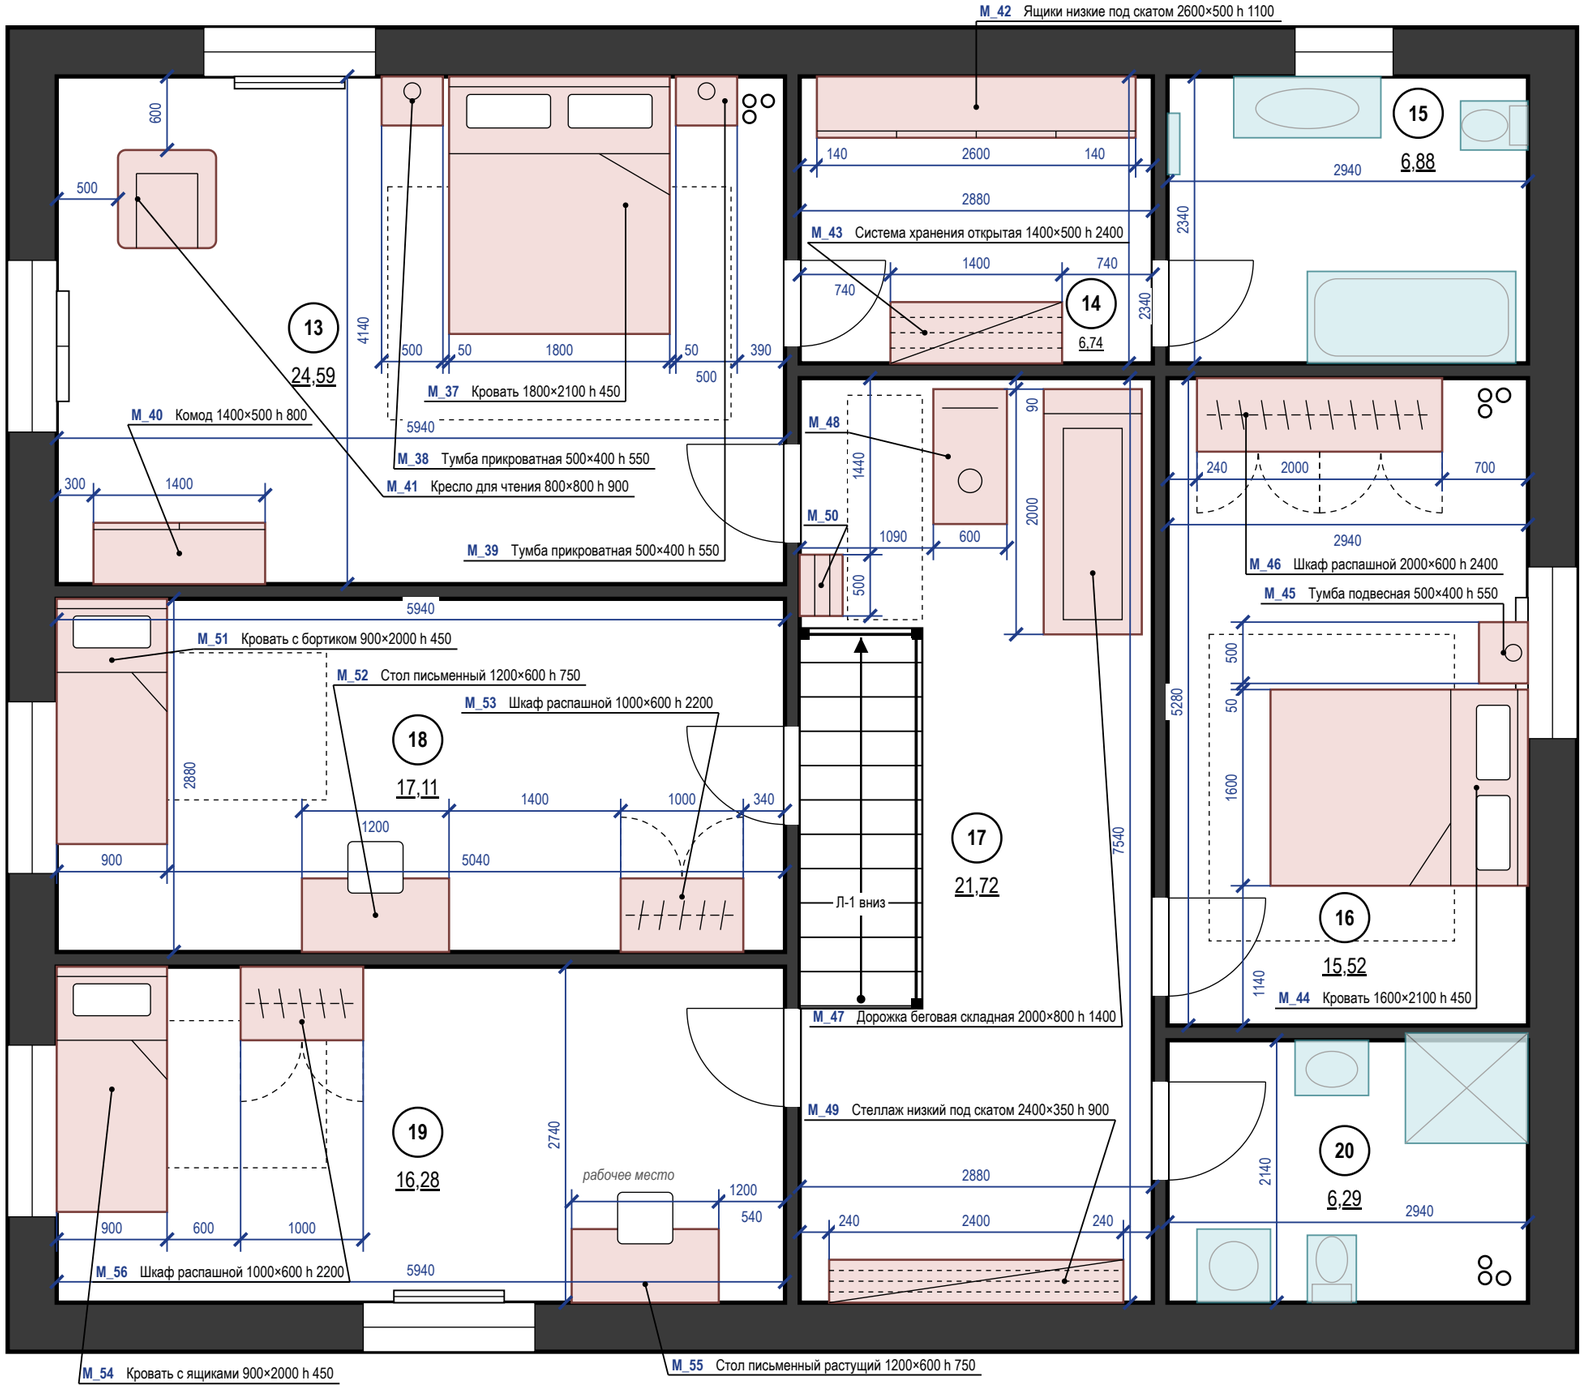

Экспликация помещений

лист 7 · на плане — номера в марках

Ведомость мебели и оборудования

Марка	Наименование	Ш×Г×В, мм	Пом.	Кол.
M_37	Кровать 1800×2000	1800×2100×450	13	1
M_38	Тумба прикроватная	500×400×550	13	1
M_39	Тумба прикроватная	500×400×550	13	1
M_40	Комод	1400×500×800	13	1
M_41	Кресло для чтения	800×800×900	13	1
M_42	Ящики низкие под скатом	2600×500×1100	14	1
M_43	Система хранения открытая	1400×500×2400	14	1
M_44	Кровать 1600×2000	1600×2100×450	16	1
M_45	Тумба подвесная	500×400×550	16	1
M_46	Шкаф распашной	2000×600×2400	16	1
M_47	Дорожка беговая складная	2000×800×1400	17	1
M_48	Велотренажёр магнитный	600×1100×1150	17	1
M_49	Стеллаж низкий под скатом	2400×350×900	17	1
M_50	Стойка-этажерка для инвентаря	500×350×1000	17	1
M_51	Кровать 900×2000 с бортиком	900×2000×450	18	1
M_52	Стол письменный	1200×600×750	18	1
M_53	Шкаф распашной	1000×600×2200	18	1
M_54	Кровать 900×2000 с ящиками	900×2000×450	19	1
M_55	Стол письменный растущий	1200×600×750	19	1
M_56	Шкаф распашной	1000×600×2200	19	1

Ш — вдоль стены (изголовья), Г — от стены (длина кровати)

Материалы, модели, допуск замены — лист 19

Примечания

1. Размеры — в мм от чистовых поверхностей стен; размеры мебели уточнить после отделочных работ; общие указания — лист 3.
2. Отступ от стены, на плане не образмерен: M_47 — 90 мм, M_48 — 90 мм.
3. У позиций M_48, M_50 на плане только марка: наименование и габарит — в спецификации, лист 19.

	Лист	№ док.	Подпись	Дата
Дизайнер	Кырлан А.С.			04.11.26

Проект: Дом 331 м² — **М 1:50**

План размещения мебели и оборудования · Мансарда

Стадия	Лист	Листов
П	18	168

Поз.	Наименование и техническая характеристика	Тип, марка, обозначение документа, опросного листа	Код продукции	Поставщик	Ед. измерения	Кол.	Масса 1 ед., кг	Примечание
	Мебель встроенная и корпусная (изготовление по чертежам мебельщика)							
M_01	Модуль под мойку у окна; корпус ЛДСП 16 мм; фасады — МДФ 18 мм, эмаль матовая; цвет фасадов — в цвет стен (NCS S 0804-Y30R); Ш×Г×В 800×600×900 мм			изготовление на заказ	шт.	1		пом. 1
M_02	Модуль под встраиваемую ПММ 60; без корпуса (ниша между соседними модулями); фасад на дверь машины — МДФ 18 мм, эмаль матовая; цоколь; цвет фасадов — в цвет стен (NCS S 0804-Y30R); Ш×Г×В 600×600×900 мм			изготовление на заказ	шт.	1		пом. 1
M_03	Модуль с ящиками; корпус ЛДСП 16 мм; фасады — МДФ 18 мм, эмаль матовая; цвет фасадов — в цвет стен (NCS S 0804-Y30R); Ш×Г×В 400×600×900 мм			изготовление на заказ	шт.	1		пом. 1
M_04	Модуль с варочной панелью и духовым шкафом; корпус ЛДСП 16 мм; фасады — МДФ 18 мм, эмаль матовая; цвет фасадов в цвет стен (NCS S 0804-Y30R); Ш×Г×В 800×600×900 мм			изготовление на заказ	шт.	1		пом. 1
M_05	Колонна с холодильником; корпус ЛДСП 16 мм; фасады — МДФ 18 мм, эмаль матовая; цвет фасадов — в цвет стен (NCS S 0804-Y30R); Ш×Г×В 700×650×2200 мм			изготовление на заказ	шт.	1		пом. 1
M_06	Модуль с ящиками; корпус ЛДСП 16 мм; фасады — МДФ 18 мм, эмаль матовая; цвет фасадов — в цвет стен (NCS S 0804-Y30R); Ш×Г×В 800×600×900 мм			изготовление на заказ	шт.	1		пом. 1
M_07	Остров с барной консолью из массива дуба, столешница — кварц; корпус ЛДСП 16 мм; фасады — МДФ 18 мм, эмаль матовая; цвет фасадов — в цвет стен (NCS S 0804-Y30R); Ш×Г×В 2000×900×900 мм			изготовление на заказ	шт.	1		пом. 1
M_09	Навесной шкаф, фасад в тон острова; корпус ЛДСП 16 мм; фасады — МДФ 18 мм, эмаль матовая; цвет фасадов — в цвет стен (NCS S 0804-Y30R); Ш×Г×В 600×350×900 мм			изготовление на заказ	шт.	1		пом. 1
M_10	Навесной шкаф узкий, полки для специй; корпус ЛДСП 16 мм; фасады — МДФ 18 мм, эмаль матовая; цвет фасадов — в цвет стен (NCS S 0804-Y30R); Ш×Г×В 400×350×900 мм			изготовление на заказ	шт.	1		пом. 1
M_11	Полки открытые из массива дуба у окна, 3 яруса; корпус ЛДСП 16 мм; фасады — МДФ 18 мм, эмаль матовая; цвет фасадов — в цвет стен (NCS S 0804-Y30R); Ш×Г×В 500×350×900 мм			изготовление на заказ	шт.	1		пом. 1
M_12	Пенал-кладовая с выдвижными корзинами; корпус ЛДСП 16 мм; фасады — МДФ 18 мм, эмаль матовая; цвет фасадов — в цвет стен (NCS S 0804-Y30R); Ш×Г×В 600×600×2200 мм			изготовление на заказ	шт.	1		пом. 1
M_17	Стеллаж технический; каркас и полки — ЛДСП 16 мм, декор «дуб натуральный»; без фасадов; Ш×Г×В 1200×400×2000 мм			изготовление на заказ	шт.	1		пом. 4
M_23	Стеллаж для хранения; каркас и полки — ЛДСП 16 мм, декор «дуб натуральный»; без фасадов; Ш×Г×В 2600×500×2200 мм			изготовление на заказ	шт.	1		пом. 7
M_24	Шкаф-купе, светлый дуб; корпус ЛДСП 16 мм; фасады — ЛДСП 10 мм в алюминиевом профиле; Ш×Г×В 1400×600×2600 мм			изготовление на заказ	шт.	1		пом. 8
M_26	Стеллаж для инструмента и шин; каркас и полки — ЛДСП 16 мм, декор «дуб натуральный»; без фасадов; Ш×Г×В 3000×500×2000 мм			изготовление на заказ	шт.	1		пом. 10; крепление к стене
M_43	Система хранения открытая в полную высоту (у перегородки, вне ската); каркас и полки — ЛДСП 16 мм, декор «дуб натуральный»; без фасадов; Ш×Г×В 1400×500×2400 мм			изготовление на заказ	шт.	1		пом. 14
M_46	Шкаф распашной, фасады — шпон ясеня с вертикальной рейкой; корпус ЛДСП 16 мм; фасады — МДФ 18 мм, эмаль матовая; цвет фасадов — в цвет стен (Farrow & Ball No. 226); Ш×Г×В 2000×600×2400 мм			изготовление на заказ	шт.	1		пом. 16
M_49	Стеллаж низкий под скатом для книг и инвентаря; каркас и полки — ЛДСП 16 мм, декор «дуб натуральный»; без фасадов; Ш×Г×В 2400×350×900 мм			изготовление на заказ	шт.	1		пом. 17; крепление к стене
M_53	Шкаф распашной, фасады — матовая эмаль шалфей; корпус ЛДСП 16 мм; фасады — МДФ 18 мм, эмаль матовая; цвет фасадов — в цвет стен (Farrow & Ball No. 226); Ш×Г×В 1000×600×2200 мм			изготовление на заказ	шт.	1		пом. 18
M_56	Шкаф распашной (вне ската), фасады — дуб и эмаль терракота; корпус ЛДСП 16 мм; фасады — МДФ 18 мм, эмаль матовая; цвет фасадов — в цвет стен (Farrow & Ball No. 226); Ш×Г×В 1000×600×2200 мм			изготовление на заказ	шт.	1		пом. 19
	Мебель покупная							
M_08	Стол обеденный 2000×1000, массив дуба; шпон, дуб натуральный, матовое масло; Ш×Г×В 2000×1000×750 мм			аналог по характеристикам	шт.	1		пом. 1; замена ≤ габарита
M_57	Стул обеденный к столу M_08; обивка — ткань, цвет Tikkurila V451; каркас — дуб натуральный; Ш×Г×В 450×500×820 мм			аналог по характеристикам	шт.	6		пом. 1; замена ≤ габарита

Примечания

1. Позиции мебели совпадают с марками на плане расстановки; размеры Ш×Г×В — Ш вдоль стены, Г от стены.
2. Размеры и привязки плана расстановки — в мм от чистовых поверхностей стен: слой штукатурки 20 мм по блоку и 5 мм шпаклёвки по ГКЛ учтён; привязки — от стен и углов помещения, а не от другой мебели.
3. План расстановки не является документацией для изготовления мебели. Встроенная и корпусная мебель изготавливается по чертежам мебельщика после контрольного обмера (после штукатурки); «стена в стену» — с зазором 10 мм с каждой стороны или с компенсаторами; графы «Тип, марка» и «Код продукции» для неё не заполняются (ГОСТ 21.110-2013).
4. Покупные изделия — аналог по характеристикам: заменять только на изделия не больше указанного габарита и того же материала и цвета.
5. Материал и цвет, не указанные в данных изделия, приняты по концепции: тон дерева — по полу, обивка — по вторичному цвету палитры; образцы согласовать до заказа.
6. Масса 1 ед. для изделий до 25 кг не указывается. Техника — по монтажным схемам изготовителя; выводы — по листам ЭОМ и ВК.

					Проект: Дом 331 м²
	Лист	№ док.	Подпись	Дата	
Дизайнер	Кырлан А.С.			04.11.26	Спецификация мебели и оборудования

Стадия	Лист	Листов
П	19	168

Поз.	Наименование и техническая характеристика	Тип, марка, обозначение документа, опросного листа	Код продукции	Поставщик	Ед. измерения	Кол.	Масса 1 ед., кг	Примечание
M_13	Письменный стол у окна, массив дуба на чёрном стальном подстолье; дерево — дуб массив, масло, металл — чёрный матовый; Ш×Г×В 1400×700×750 мм			аналог по характеристикам	шт.	1		пом. 2; замена ≤ габарита
M_14	Кресло рабочее на колёсах, кожа коньячная; обивка кожа натуральная, коньяк; Ш×Г×В 600×600×900 мм			аналог по характеристикам	шт.	1		пом. 2; замена ≤ габарита
M_15	Диван-кровать гостевой, шерстяной твид; обивка шерстяной твид, серо-оливковый меланж; Ш×Г×В 2000×900×850 мм			аналог по характеристикам	шт.	1		пом. 2; замена ≤ габарита
M_16	Стеллаж для книг, чёрная сталь и полки из дуба; каркас — чёрная сталь, полки — массив дуба; Ш×Г×В 1600×400×2200 мм			аналог по характеристикам	шт.	1		пом. 2; крепление к стене; замена ≤ габарита
M_18	Диван угловой, лён-рогожка; обивка лён-рогожка плотный, молочный; Ш×Г×В 3200×1000×820 мм			аналог по характеристикам	шт.	1		пом. 5; замена ≤ габарита
M_19	Столик журнальный, столешница — сланец, подстолье дуб; столешница — сланец 20 мм, подстолье — массив дуба; Ш×Г×В 1200×700×420 мм			аналог по характеристикам	шт.	1		пом. 5; замена ≤ габарита
M_20	Кресло, букле (овечья шерсть); обивка букле, овечья шерсть, молочный; Ш×Г×В 850×850×850 мм			аналог по характеристикам	шт.	1		пом. 5; замена ≤ габарита
M_21	Кресло-качалка, кожа и ясень; обивка кожа натуральная, тёмный коньяк, дерево — ясень гнутый; Ш×Г×В 850×850×850 мм			аналог по характеристикам	шт.	1		пом. 5; замена ≤ габарита
M_22	Буфет низкий, дуб; шпон, дуб натуральный, матовое масло; Ш×Г×В 1600×450×800 мм			аналог по характеристикам	шт.	1		пом. 5; крепление к стене; замена ≤ габарита
ОБ_01	ТВ-стена с камином, облицовка — колотый сланец; короб ГКЛ с облицовкой колотым сланцем, полка из массива дуба; Ш×Г×В 2400×450×600 мм			аналог по характеристикам	шт.	1		пом. 5; замена ≤ габарита
M_25	Банкетка; Ш×Г×В 1000×400×450 мм			аналог по характеристикам	шт.	1		пом. 8; замена ≤ габарита
M_27	Силовая стойка со скамьёй и штангой; стальная рама, порошковая окраска, чёрный матовый; под тренажёр — резиновый коврик 10 мм; Ш×Г×В 1200×1500×2300 мм			аналог по характеристикам	шт.	1		пом. 10; замена ≤ габарита
M_28	Верстак с перфопанелью; шпон, дуб натуральный, матовое масло; Ш×Г×В 1800×700×900 мм			аналог по характеристикам	шт.	1		пом. 10; замена ≤ габарита
M_29	Тренажёр гребной магнитный, складной; алюминиевая направляющая, маховик магнитный или водяной, сиденье на роликах; под тренажёр — резиновый коврик 10 мм; Ш×Г×В 2400×600×500 мм			аналог по характеристикам	шт.	1		пом. 10; замена ≤ габарита
M_30	Стойка для гантелей 2 яруса, пары 4–20 кг; стальная рама, порошковая окраска, чёрный матовый; гантели с обрезиненными дисками; Ш×Г×В 1000×500×800 мм			аналог по характеристикам	шт.	1		пом. 10; крепление к стене; замена ≤ габарита
M_31	Стенка шведская, бук, с навесным турником; массив бука, лак матовый; перекладины Ø40 шаг 200; крепление к стене — анкеры по основанию, не менее 6; Ш×Г×В 900×150×2300 мм			аналог по характеристикам	шт.	1		пом. 10; крепление к стене; замена ≤ габарита
M_32	Стол летний; шпон, дуб натуральный, матовое масло; Ш×Г×В 1600×900×750 мм			аналог по характеристикам	шт.	1		пом. 11; замена ≤ габарита
M_33	Диван плетёный; обивка — ткань, цвет Tikkurila V451; Ш×Г×В 2000×800×800 мм			аналог по характеристикам	шт.	1		пом. 11; замена ≤ габарита
M_34, M_35	Кресло плетёное; обивка — ткань, цвет Tikkurila V451; Ш×Г×В 800×800×800 мм			аналог по характеристикам	шт.	2		пом. 11; замена ≤ габарита
M_36	Столик кофейный из тика; шпон, дуб натуральный, матовое масло; Ш×Г×В 1000×600×420 мм			аналог по характеристикам	шт.	1		пом. 11; замена ≤ габарита
M_58	Стул обеденный к столу M_32; обивка — ткань, цвет Tikkurila V451; каркас — дуб натуральный; Ш×Г×В 450×500×820 мм			аналог по характеристикам	шт.	6		пом. 11; замена ≤ габарита
M_37	Кровать 1800×2000, изголовье — мягкое в шерстяном твиде; обивка шерстяной твид, серо-коричневый, дерево — дуб массив, царги и ножки; Ш×Г×В 1800×2100×450 мм			аналог по характеристикам	шт.	1		пом. 13; замена ≤ габарита
M_38, M_39	Тумба прикроватная, массив ореха; дерево — орех массив, масло; Ш×Г×В 500×400×550 мм			аналог по характеристикам	шт.	2		пом. 13; замена ≤ габарита
M_40	Комод, дуб брашированный, фасады с кожаными ручками; дерево — дуб брашированный, масло; Ш×Г×В 1400×500×800 мм			аналог по характеристикам	шт.	1		пом. 13; крепление к стене; замена ≤ габарита
M_41	Кресло для чтения, букле (овечья шерсть); обивка букле, овечья шерсть, молочный; Ш×Г×В 800×800×900 мм			аналог по характеристикам	шт.	1		пом. 13; замена ≤ габарита
M_42	Ящики низкие под скатом (до колена 1200); шпон, дуб натуральный, матовое масло; Ш×Г×В 2600×500×1100 мм			аналог по характеристикам	шт.	1		пом. 14; замена ≤ габарита
M_44	Кровать 1600×2000, изголовье — вертикальная рейка из ясеня; дерево — ясень массив, рейка; Ш×Г×В 1600×2100×450 мм			аналог по характеристикам	шт.	1		пом. 16; замена ≤ габарита

					Проект: Дом 331 м²	
	Лист	№ док.	Подпись	Дата	Спецификация мебели и оборудования (продолжение)	Стадия: П; Лист: 20; Листов: 168
Дизайнер	Кырлан А.С.			04.11.26		

Поз.	Наименование и техническая характеристика	Тип, марка, обозначение документа, опросного листа	Код продукции	Поставщик	Ед. измерения	Кол.	Масса 1 ед., кг	Примечание
M_45	Тумба подвесная, ясень; дерево — ясень шпон; Ш×Г×В 500×400×550 мм			аналог по характеристикам	шт.	1		пом. 16; крепление к стене; замена ≤ габарита
M_47	Дорожка беговая складная, полотно 1400×500; стальная рама, порошковая окраска, чёрный матовый; под тренажёр резиновый коврик 10 мм; Ш×Г×В 2000×800×1400 мм			аналог по характеристикам	шт.	1		пом. 17; замена ≤ габарита
M_48	Велотренажёр магнитный; стальная рама, порошковая окраска, чёрный матовый; под тренажёр — резиновый коврик 10 мм; Ш×Г×В 600×1100×1150 мм			аналог по характеристикам	шт.	1		пом. 17; замена ≤ габарита
M_50	Стойка-этажерка для инвентаря: гантели 2–8 кг, эспандеры, ролик; стальная рама, порошковая окраска, чёрный матовый; гантели с обрезиненными дисками; Ш×Г×В 500×350×1000 мм			аналог по характеристикам	шт.	1		пом. 17; крепление к стене; замена ≤ габарита
M_51	Кровать 900×2000 с бортиком, массив сосны; дерево — сосна массив, воск; Ш×Г×В 900×2000×450 мм			аналог по характеристикам	шт.	1		пом. 18; замена ≤ габарита
M_52	Стол письменный, столешница ЛДСП светлый ясень, ножки — белая сталь; столешница ЛДСП «светлый ясень», ножки сталь, белая эмаль; Ш×Г×В 1200×600×750 мм			аналог по характеристикам	шт.	1		пом. 18; замена ≤ габарита
M_54	Кровать 900×2000 с ящиками, массив берёзы; дерево — берёза массив, масло; Ш×Г×В 900×2000×450 мм			аналог по характеристикам	шт.	1		пом. 19; замена ≤ габарита
M_55	Стол письменный растущий, берёзовая фанера на регулируемом каркасе; столешница — берёзовая фанера, лак; каркас сталь, тёмно-серая эмаль, регулировка 600–800; Ш×Г×В 1200×600×750 мм			аналог по характеристикам	шт.	1		пом. 19; замена ≤ габарита
	Техника встраиваемая и бытовая (покупные изделия), светильники под розетки							
	Посудомоечная машина встраиваемая, в модуле M_02; ниша 600 мм	аналог по характеристикам: полновстраиваемая 60 см под фасад, ниша 600 × 862 мм, навеска фасада в комплекте		по выбору заказчика до изготовления мебели	шт.	1		пом. 1; по схеме изготовителя
	Варочная панель встраиваемая, индукционная, в модуле M_04	аналог по характеристикам: индукционная 60 см, вырез 560 × 490 мм по шаблону модели		по выбору заказчика до изготовления мебели	шт.	1		пом. 1; по схеме изготовителя
	Духовой шкаф встраиваемый, в модуле M_04	аналог по характеристикам: 60 см, лицевая панель 595 мм, ниша 560 × 600, глубина ≥ 550 мм, вентиляция за прибором		по выбору заказчика до изготовления мебели	шт.	1		пом. 1; по схеме изготовителя
	Холодильник встраиваемый, в модуле M_05	аналог по характеристикам: полновстраиваемый под фасад, ниша 1780 × 560 × 550 мм, вентиляция решётка в цоколе, выход сверху		по выбору заказчика до изготовления мебели	шт.	1		пом. 1; по схеме изготовителя
	Вытяжка встраиваемая, над модулем M_01 — предложено	аналог по характеристикам: производительность — по расчёту ОВ, шум ≤ 55 дБ(А)		по выбору заказчика до изготовления мебели	шт.	1		пом. 1; предложено, решает заказчик; вывод P21 (ЭОМ)
	Стиральная машина — предложено	аналог по характеристикам: тип загрузки — по листу ВК, по листу ВК		по выбору заказчика до изготовления мебели	шт.	1		пом. 3; предложено, решает заказчик; вывод P7 (ЭОМ)
	Стиральная машина — предложено	аналог по характеристикам: тип загрузки — по листу ВК, по листу ВК		по выбору заказчика до изготовления мебели	шт.	1		пом. 15; предложено, решает заказчик; вывод P48 (ЭОМ)
	Стиральная машина, место по листу ВК (ОБ_02); Ш×Г 600×600 мм	аналог по характеристикам: тип загрузки — по листу ВК, в плане 600 × 600 мм (ширина × глубина), по листу ВК		по выбору заказчика до изготовления мебели	шт.	1		пом. 20; по схеме изготовителя
	Торшер, у поз. M_40; абажур — ткань или опаловое стекло; лампа 2700 K			аналог по характеристикам	шт.	1		пом. 13; розетка P46 (ЭОМ)
	Текстиль							
T14	Рулонная штора кассетная, ткань димаут; полиэстер 100 %; цвет NCS S 2005-Y20R; карниз 890 мм, высота 2000 мм			аналог по характеристикам	шт.	1		пом. 1
T7	Портьеры на люверсах, шерстяной твид; лён 100 %; цвет Farrow & Ball No. 40; карниз 1820 мм, высота 2790 мм, сборка 2			аналог по характеристикам	шт.	2		пом. 2
T8	Тюль, льняная сетка; полиэстер 100 %; цвет NCS S 0804-Y30R; карниз 1820 мм, высота 2790 мм, сборка 2,5			аналог по характеристикам	шт.	1		пом. 2
T9	Ковёр джутовый под диваном; шерсть 100 %; цвет Tikkurila X463; 1700×2300 мм			аналог по характеристикам	шт.	1		пом. 2; с подложкой
T10	Подушки на диван, кожа; букле (шерсть 60 %, полиэстер 40 %); цвет NCS S 3010-Y30R			аналог по характеристикам	шт.	3		пом. 2

	Лист	№ док.	Подпись	Дата	
Дизайнер	Кырлан А.С.			04.11.26	Спецификация мебели и оборудования (продолжение)

Проект: Дом 331 м²

Стадия	Лист	Листов
П	21	168

Поз.	Наименование и техническая характеристика	Тип, марка, обозначение документа, опросного листа	Код продукции	Поставщик	Ед. измерения	Кол.	Масса 1 ед., кг	Примечание
T11	Подушки на кровать, акцент; хлопковый бархат 100 %; цвет Farrow & Ball No. 298			аналог по характеристикам	шт.	2		пом. 2
T12	Плед на кровать; шерсть мериноса 100 %; цвет Farrow & Ball No. 298			аналог по характеристикам	шт.	1		пом. 2
T1	Портьеры-волна, два полотна; лён 100 %; цвет NCS S 2005-Y20R; карниз 2150 мм, высота 2710 мм, сборка 2			аналог по характеристикам	шт.	2		пом. 5
T2	Тюль-вуаль, одно полотно; полиэстер 100 %; цвет NCS S 0804-Y30R; карниз 2150 мм, высота 2710 мм, сборка 2,5			аналог по характеристикам	шт.	1		пом. 5
T3	Ковёр мягкой группы, шерсть с джутом; шерсть 100 %; цвет Farrow & Ball No. 243; 3600×2400 мм			аналог по характеристикам	шт.	1		пом. 5; с подложкой
T4	Подушки декоративные на диван, лён; лён 100 %; цвет Farrow & Ball No. 226			аналог по характеристикам	шт.	3		пом. 5
T5	Подушки декоративные на диван, акцент; хлопковый бархат 100 %; цвет Farrow & Ball No. 93			аналог по характеристикам	шт.	2		пом. 5
T6	Плед на диван; шерсть мериноса 100 %; цвет Farrow & Ball No. 93			аналог по характеристикам	шт.	1		пом. 5
T40	Покрытие резиновое модульное 500×500×10 мм под спортзону; резиновая крошка SBR с цветными EPDM-вкраплениями, плиты 500×500, 10 мм; цвет Farrow & Ball No. 243; 1500×6300 мм			аналог по характеристикам	шт.	1		пом. 10
T13	Портьеры-волна, шерсть с блэкаут-подкладкой; лён 100 %; цвет Farrow & Ball No. 229; карниз 1800 мм, высота 2590 мм, сборка 2			аналог по характеристикам	шт.	2		пом. 13
T15	Тюль; полиэстер 100 %; цвет Little Greene No. 105; карниз 1800 мм, высота 2590 мм, сборка 2,5			аналог по характеристикам	шт.	1		пом. 13
T16	Ковёр под кроватью, шерсть ручного ткачества; шерсть 80 %, хлопок 20 %; цвет NCS S 2005-Y20R; 2800×1900 мм			аналог по характеристикам	шт.	1		пом. 13; с подложкой
T17	Подушки декоративные на кровать, шерсть-меланж; лён 100 %; цвет NCS S 2005-Y20R			аналог по характеристикам	шт.	3		пом. 13
T18	Подушки на кровать, акцент; хлопковый бархат 100 %; цвет NCS S 7020-G10Y			аналог по характеристикам	шт.	2		пом. 13
T19	Плед на кровать; шерсть мериноса 100 %; цвет NCS S 7020-G10Y			аналог по характеристикам	шт.	1		пом. 13
T20	Портьеры-волна, хлопок-сатин с блэкаут-подкладкой; лён 100 %; цвет Tikkurila X463; карниз 1820 мм, высота 2690 мм, сборка 2			аналог по характеристикам	шт.	2		пом. 16
T21	Тюль, лён-вуаль; полиэстер 100 %; цвет Little Greene No. 105; карниз 1820 мм, высота 2690 мм, сборка 2,5			аналог по характеристикам	шт.	1		пом. 16
T22	Ковёр под кроватью, шерсть с узором ромбы; шерсть 100 %; цвет NCS S 3010-Y30R; 2000×2500 мм			аналог по характеристикам	шт.	1		пом. 16; с подложкой
T23	Подушки декоративные на кровать, хлопок-рогожка; букле (шерсть 60 %, полиэстер 40 %); цвет Tikkurila X463			аналог по характеристикам	шт.	3		пом. 16
T24	Подушки на кровать, акцент; хлопковый бархат 100 %; цвет Farrow & Ball No. 64			аналог по характеристикам	шт.	2		пом. 16
T25	Плед на кровать; шерсть мериноса 100 %; цвет Farrow & Ball No. 64			аналог по характеристикам	шт.	1		пом. 16
T41	Коврик для йоги и растяжки 1830×610×6, TPE, нескользящий; TPE, 6 мм, двухслойный; цвет NCS S 3020-G30Y; 610×1830 мм			аналог по характеристикам	шт.	1		пом. 17
T26	Портьеры на люверсах, хлопок-канвас с блэкаут-подкладкой; лён 100 %; цвет Tikkurila V451; карниз 1820 мм, высота 2610 мм, сборка 2			аналог по характеристикам	шт.	2		пом. 18
T27	Тюль, хлопковая кисея; полиэстер 100 %; цвет NCS S 0804-Y30R; карниз 1820 мм, высота 2610 мм, сборка 2,5			аналог по характеристикам	шт.	1		пом. 18
T28	Ковёр под кроватью, хлопок, стираемый; шерсть 100 %; цвет NCS S 2005-Y20R; 1600×1200 мм			аналог по характеристикам	шт.	1		пом. 18; с подложкой
T29	Подушки на кровать, хлопок-вельвет; букле (шерсть 60 %, полиэстер 40 %); цвет Tikkurila V451			аналог по характеристикам	шт.	3		пом. 18
T30	Подушки на кровать, акцент; хлопковый бархат 100 %; цвет NCS S 3020-G30Y			аналог по характеристикам	шт.	2		пом. 18
T31	Плед на кровать; шерсть мериноса 100 %; цвет NCS S 3020-G30Y			аналог по характеристикам	шт.	1		пом. 18
T32	Портьеры-волна, лён-меланж с блэкаут-подкладкой; лён 100 %; цвет NCS S 2005-Y20R; карниз 1800 мм, высота 2590 мм, сборка 2			аналог по характеристикам	шт.	2		пом. 19
T33	Тюль, лён-вуаль в мелкую клетку; полиэстер 100 %; цвет Farrow & Ball No. 226; карниз 1800 мм, высота 2590 мм, сборка 2,5			аналог по характеристикам	шт.	1		пом. 19
T34	Ковёр под кроватью, шерсть с узором «горы»; шерсть 100 %; цвет NCS S 3010-Y30R; 1600×1200 мм			аналог по характеристикам	шт.	1		пом. 19; с подложкой
T35	Подушки на кровать, хлопок-канвас с принтом; букле (шерсть 60 %, полиэстер 40 %); цвет Tikkurila X463			аналог по характеристикам	шт.	3		пом. 19
T36	Подушки на кровать, акцент; хлопковый бархат 100 %; цвет NCS S 3040-Y70R			аналог по характеристикам	шт.	2		пом. 19

					Проект: Дом 331 м²
	Лист	№ док.	Подпись	Дата	
Дизайнер	Кырлан А.С.			04.11.26	Спецификация мебели и оборудования (продолжение)

Стадия	Лист	Листов
П	22	168

Поз.	Наименование и техническая характеристика	Тип, марка, обозначение документа, опросного листа	Код продукции	Поставщик	Ед. измерения	Кол.	Масса 1 ед., кг	Примечание
Т37	Плед на кровать; шерсть мериноса 100 %; цвет NCS S 3040-Y70R			аналог по характеристикам	шт.	1		пом. 19
	Декор							
ДК8	Часы настенные Ø400; 400×400 мм; центр на 1550 мм от пола			аналог по характеристикам	шт.	1	2	пом. 1; крепление: дюбель с крюком, 1 точка
ДК9	Хлорофитум хохлатый на подоконнике (отм. +0,800); 300×200 мм; низ на 800 мм от пола			аналог по характеристикам	шт.	1		пом. 1
ДК23	Ваза с тюльпанами на обеденном столе; 200×350 мм; на M_08			аналог по характеристикам	шт.	1		пом. 1
ДК3	Картина над диваном: офорт в паспарту, рама — орех; 1000×700 мм; низ на 1100 мм от пола			аналог по характеристикам	шт.	1	4	пом. 2; крепление к стене
ДК28	Замиокулькас в кашпо Ø350; 350×350 мм			аналог по характеристикам	шт.	1		пом. 2
ДК1	Картина над буфетом: пейзаж, масло, рама — морёный дуб; 1200×900 мм; низ на 1000 мм от пола			аналог по характеристикам	шт.	1	6	пом. 5; крепление: планка на дюбелях, 4 точки
ДК2	Фикус лировидный в кашпо Ø400; 450×450 мм			аналог по характеристикам	шт.	1		пом. 5
ДК21	Оливковое дерево в кашпо Ø450; 450×450 мм			аналог по характеристикам	шт.	1		пом. 5
ДК22	Ваза с живыми цветами на журнальном столе; 200×350 мм; на M_19			аналог по характеристикам	шт.	1		пом. 5
ДК5	Зеркало; рама — чёрный матовый; 800×1800 мм; низ на 550 мм от пола			аналог по характеристикам	шт.	1	18	пом. 8; крепление: анкер, 4 шт.
ДК31	Зеркало 1200×1500 для контроля техники, безопасное (плёнка), без рамы; 1200×1500 мм; низ на 600 мм от пола			аналог по характеристикам	шт.	1	22	пом. 10; крепление: анкер, 4 шт.
ДК24	Гортензия крупнолистная в кадке Ø500; 500×500 мм			аналог по характеристикам	шт.	1		пом. 11
ДК25	Самшит в кадке Ø450; 450×450 мм			аналог по характеристикам	шт.	1		пом. 11
ДК26	Папоротник нефролепис в ящике 600×250; 250×600 мм			аналог по характеристикам	шт.	1		пом. 11
ДК4	Картина над кроватью: акварель, рама — лиственница; 1000×700 мм; низ на 1300 мм от пола			аналог по характеристикам	шт.	1	4	пом. 13; крепление к стене
ДК27	Фикус каучуконосный в кашпо Ø400; 400×400 мм			аналог по характеристикам	шт.	1		пом. 13
ДК6	Картина над кроватью: натюрморт, масло, рама — тонкая латунь; 1000×700 мм; низ на 1300 мм от пола			аналог по характеристикам	шт.	1	4	пом. 16; крепление к стене
ДК7	Зеркало в рост в раме из ясеня; рама — чёрный матовый; 600×1600 мм; низ на 300 мм от пола			аналог по характеристикам	шт.	1	12	пом. 16; крепление: анкер для пустотелых оснований, 4 шт.
ДК30	Монстера в кашпо Ø450 с фитолампой; 450×450 мм			аналог по характеристикам	шт.	1		пом. 17
ДК10	Картина над кроватью: детская иллюстрация, рама — светлый ясень; 600×700 мм; низ на 1100 мм от пола			аналог по характеристикам	шт.	1	4	пом. 18; крепление к стене
ДК11	Зеркало безопасное (плёнка), рама — светлый ясень; рама — чёрный матовый; 500×1600 мм; низ на 300 мм от пола			аналог по характеристикам	шт.	1	12	пом. 18; крепление: анкер для пустотелых оснований, 4 шт.
ДК12	Картина над кроватью: детский принт, рама — белёный дуб; 600×700 мм; низ на 1100 мм от пола			аналог по характеристикам	шт.	1	4	пом. 19; крепление к стене
ДК13	Зеркало круглое Ø600 в кожаном ремне; рама — чёрный матовый; 600×600 мм; низ на 1150 мм от пола			аналог по характеристикам	шт.	1	12	пом. 19; крепление: анкер для пустотелых оснований, 4 шт.

					Проект: Дом 331 м²	
	Лист	№ док.	Подпись	Дата		
Дизайнер	Кырлан А.С.			04.11.26	Спецификация мебели и оборудования (продолжение)	Стадия: П; Лист: 23; Листов: 168

Ведомость изделий

Марка	Наименование	Пом.	Ш×Г×В, мм	Корпус	Фасад	Кромка, мм	Кол.
M_17	Система хранения	4	1200×400×2000	ЛДСП 16	без фасадов	0,4 / 2	1
M_23	Система хранения	7	2600×500×2200	ЛДСП 16	без фасадов	0,4 / 2	1
M_24	Шкаф-купе	8	1400×600×2600	ЛДСП 16	ЛДСП 10 мм в алюминиевом профиле	0,4 / 2	1
M_26	Система хранения	10	3000×500×2000	ЛДСП 16	без фасадов	0,4 / 2	1
M_43	Система хранения	14	1400×500×2400	ЛДСП 16	без фасадов	0,4 / 2	1
M_46	Шкаф распашной	16	2000×600×2400	ЛДСП 16	МДФ 18 мм, эмаль матовая	0,4 / 2	1
M_49	Система хранения	17	2400×350×900	ЛДСП 16	без фасадов	0,4 / 2	1
M_53	Шкаф распашной	18	1000×600×2200	ЛДСП 16	МДФ 18 мм, эмаль матовая	0,4 / 2	1
M_56	Шкаф распашной	19	1000×600×2200	ЛДСП 16	МДФ 18 мм, эмаль матовая	0,4 / 2	1
M_06	Модуль нижний: ящики	1	800×600×900	ЛДСП 16	МДФ 18 мм, эмаль матовая	0,4 / 2	1
M_11	Модуль навесной: полки	1	500×350×900	ЛДСП 16	МДФ 18 мм, эмаль матовая	0,4 / 2	1
M_01	Модуль нижний: мойка	1	800×600×900	ЛДСП 16	МДФ 18 мм, эмаль матовая	0,4 / 2	1
M_02	Модуль под ПММ 60: без корпуса, фасад на дверь машины	1	600×600×900	без корпуса	МДФ 18 мм, эмаль матовая — на дверь машины (навеска из её комплекта), цоколь		1
M_09	Модуль навесной: полки	1	600×350×900	ЛДСП 16	МДФ 18 мм, эмаль матовая	0,4 / 2	1
M_03	Модуль нижний: ящики	1	400×600×900	ЛДСП 16	МДФ 18 мм, эмаль матовая	0,4 / 2	1
M_04	Модуль нижний: духовой шкаф, варочная	1	800×600×900	ЛДСП 16	МДФ 18 мм, эмаль матовая	0,4 / 2	1
M_10	Модуль навесной: полки	1	400×350×900	ЛДСП 16	МДФ 18 мм, эмаль матовая	0,4 / 2	1
M_05	Пенал: холодильник встр.	1	700×650×2200	ЛДСП 16	МДФ 18 мм, эмаль матовая	0,4 / 2	1
M_12	Пенал: полки	1	600×600×2200	ЛДСП 16	МДФ 18 мм, эмаль матовая	0,4 / 2	1
M_07	Остров (M_07.1, M_07.2, M_07.3)	1	2000×900×900	ЛДСП 16	МДФ 18 мм, эмаль матовая	0,4 / 2	1

Ведомость встраиваемой техники

Поз.	Прибор	Ниша, вырез, мм	Вентиляция	Питание	Схема
M_01	Мойка врезная / подстольная с сифоном	вырез по шаблону, ориентир 700 × 480		смеситель — выводы ВК	по модели
M_02	Посудомоечная машина встраиваемая, 60 см	ниша 600 × 862 (от пола до низа столешницы)	зазор в цоколе, по схеме	питание: точка ЭОМ не задана — вывод под прибор не делать до задания	по модели
M_04	Духовой шкаф встраиваемый, 60 см	ниша 560 × 600, глубина ≥ 550	зазор за шкафом, вырез в задней стенке	питание: точка ЭОМ не задана — вывод под прибор не делать до задания	по модели
M_04	Варочная панель индукционная, 60 см	вырез в столешнице 560 × 490		питание: точка ЭОМ не задана — вывод под прибор не делать до задания	по модели
M_05	Холодильник встраиваемый, ниша 1780	ниша 1780 × 560 × 550	решётка в цоколе, канал за корпусом, выход сверху	питание: точка ЭОМ не задана — вывод под прибор не делать до задания	по модели
M_04	Вытяжка настенная, 60 см	низ ≥ 650 над панелью	воздуховод к вентканалу, короб до потолка	вывод кабеля в коробе	по модели

Ведомость фурнитуры


№	Фурнитура	Тип, размер	Изделия	Кол.
1	Штанга выдвижная торцевая	L по глубине	M_17, M_23, M_26, M_43	6
2	Полкодержатель с фиксацией	ø5 мм	M_17, M_23, M_24, M_26, M_43, M_46, M_49, M_53, M_56, M_11, M_09, M_10, M_05, M_12, M_07	252
3	Опора регулируемая с цоколем на клипсах	ход 20 мм	M_17, M_23, M_24, M_26, M_43, M_46, M_49, M_53, M_56	66
4	Анкер по основанию стены	по таблице крепежа	M_17, M_23, M_24, M_26, M_43, M_46, M_49, M_53, M_56, M_11, M_09, M_10	75
5	Уголок крепления к стене от опрокидывания	стальной	M_17, M_23, M_24, M_26, M_43, M_46, M_49, M_53, M_56, M_05, M_12	22
6	Система дверей купе: профиль, направляющие, ролики	на 2 двери	M_24	1
7	Ручка-профиль вертикальная	в цвет профиля	M_24	2
8	Штанга овальная 30×15, L = 676	+ 2 держателя	M_24	1
9	Полка для обуви выдвижная наклонная	ширина 676	M_24	3
10	Петля накладная 110° с доводчиком	чашка 35 мм	M_46, M_53, M_56, M_11, M_01, M_09, M_10, M_05, M_12	72
11	Штанга овальная 30×15, L = 976	+ 2 держателя	M_46	1
12	Штанга овальная 30×15, L = 968	+ 2 держателя	M_53, M_56	2
13	Направляющие полного выдвижения с доводчиком NL 500	пара	M_06, M_03, M_04, M_07	16
14	Ручка-профиль	латунь матовая	M_06, M_11, M_01, M_02, M_09, M_03, M_04, M_10, M_05, M_12, M_07	28
15	Опора кухонная регулируемая 100–120 мм	+ клипса цоколя	M_06, M_01, M_03, M_04, M_05, M_12, M_07	50
16	Навес регулируемый для навесного шкафа	пара на секцию	M_11, M_09, M_10	3
17	Шина монтажная	L = 440	M_11	1
18	Комплект навески фасада ПММ	из поставки машины	M_02	1
19	Шина монтажная	L = 540	M_09	1
20	Шина монтажная	L = 340	M_10	1
21	Уголок крепления острова к полу	стальной, в цоколе	M_07	4

Примечания


1. Модели техники выбирает заказчик до изготовления мебели; ниши, вырезы и вентиляция — по монтажной схеме выбранной модели (условие гарантии), её номер вносится в ведомость.
2. Количество фурнитуры — по чертежам изделий; запас крепежа 5 %. Аналоги — по характеристикам (доводчик, нагрузка, ход).
3. Цвет корпусов, фасадов и профилей — по колерной карте проекта. Кромка — скрытые / видимые торцы, мм.

					Проект: Дом 331 м²			
	Лист	№ док.	Подпись	Дата	Ведомости изделий, техники и фурнитуры	Стадия	Лист	Листов
Дизайнер	Кырлан А.С.			04.11.26		П	24	168

Фрагмент 1. Санузел 1 этажа (пом. 3)

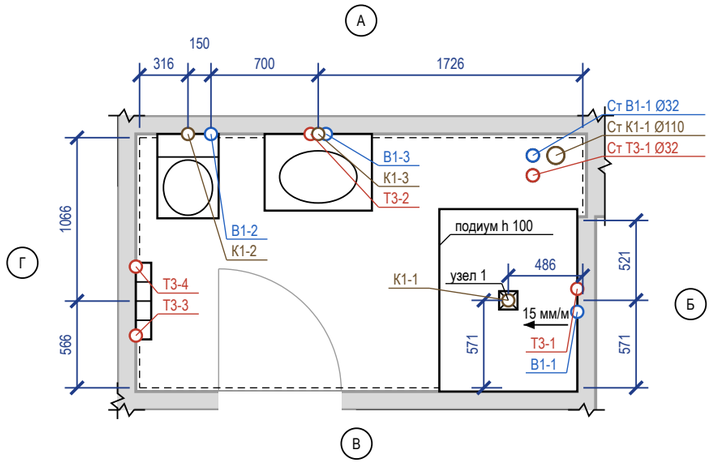

Фрагмент 2. Кухня-столовая (пом. 1)

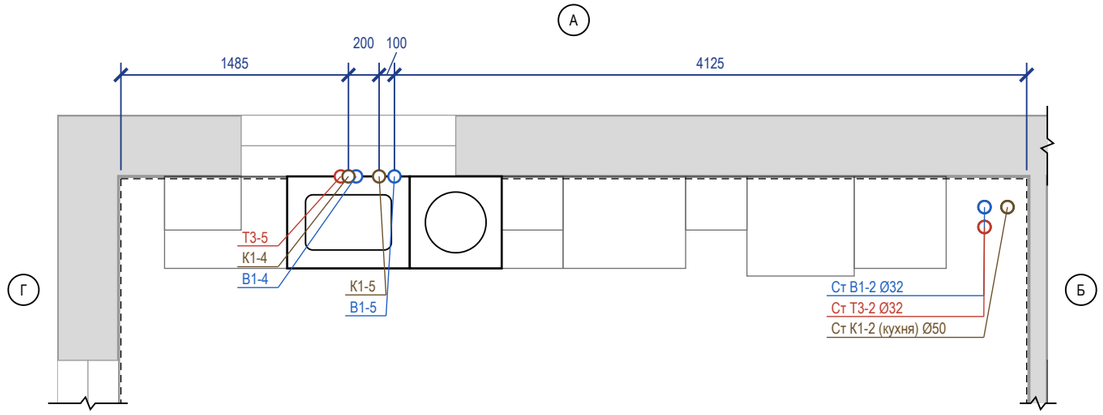

Ведомость привязок выводов

Код	Прибор	Ø	H, мм	Привязка от чист. стен, мм	Прим.
В1-1	С_01 душ	½"	1300	ст. Б: 496 от В	межос. 150; 1200 от пола душа (подиум 100, +0,085)
Т3-1	С_01 душ	½"	1300	ст. Б: 446 от В	межос. 150; 1200 от пола душа (подиум 100, +0,085)
К1-1	С_01 душ	Ø50	100	486 от Б; 571 от В	трап в подиуме 100
В1-2	С_02 унитаз подвесной	½"	250	ст. А: 466 от Г	в раме инсталляции
К1-2	С_02 унитаз подвесной	Ø110	220	ст. А: 316 от Г	
В1-3	С_03 умывальник	½"	600	ст. А: 1216 от Г	межос. 100
Т3-2	С_03 умывальник	½"	600	ст. А: 1116 от Г	межос. 100
К1-3	С_03 умывальник	Ø50	500	ст. А: 1166 от Г	
Т3-3	С_04 полотенцесушитель	½"	1150	ст. Г: 341 от В	подача, межос. 450; байпас и краны
Т3-4	С_04 полотенцесушитель	½"	1150	ст. Г: 791 от В	обратка
В1-4	М_01 мойка кухонная	½"	600	ст. А: 1535 от Г	межос. 100
Т3-5	М_01 мойка кухонная	½"	600	ст. А: 1435 от Г	межос. 100
К1-4	М_01 мойка кухонная	Ø50	400	ст. А: 1485 от Г	
В1-5	М_02 посудомоечная машина	½"	550	ст. А: 1785 от Г	кран ПММ в шкафу мойки
К1-5	М_02 посудомоечная машина	Ø40	550	ст. А: 1685 от Г	слив ПММ в шкафу мойки

Условные обозначения


- вывод В1 (код — в ведомости привязок)
- вывод Т3 (код — в ведомости привязок)
- вывод К1 (код — в ведомости привязок)
- сантехприбор по расстановке (габарит модели)
- чистовая поверхность стены (от неё привязки)
- стояк «Ст К1-N / Ст В1-N» (ГОСТ 21.601), Ø мм
- линия обрыва (граница фрагмента)
- трап / лоток в полу
- направление уклона К1 / пола: Ø, мм на 1 м
- А — обозначение стены А–Г (как на развёртках)

Примечания


1. Привязки выводов даны от чистовых поверхностей стен (облицовка на сторону: санузел 1 этажа — 24 мм (штукатурка 10 + клей 5 + плитка 9); кухня-столовая — 22 мм (фартук: штукатурка 10 + клей 3 + плитка 9)); эти же грани — на развёртках и в раскладке плитки. Высоты — от чистого пола помещения.
2. До черновой разводки сверить по паспорту выбранного прибора (смеситель, инсталляция, сифон).
3. Горячая вода (Т3) — слева от холодной (В1), если смотреть на прибор. Допуск установки выводов: ±5 мм в группе, ±20 мм у отдельно стоящих.
4. Расчёт систем водоснабжения и канализации и подбор оборудования выполняет проектная организация; лист задаёт места и высоты выводов.
5. С_01 душ (В1-1, Т3-1, К1-1): трап в подиуме 100 мм — верх подиума у решётки трапа +0,085, к краю поднимается уклоном 15 мм/м: ступень по открытому краю 109 мм (край показан на плане); «узел 1» — на схеме разводки; подиум — предложение, согласовать с заказчиком. Водорозетки В1-1, Т3-1 — 1200 мм от пола душа, то есть 1300 мм от чистого пола помещения: стену размечают до подиума.
6. Посудомоечная машина М_02: кран и слив — отдельными выводами в шкафу мойки (не за машиной), до машины ≤ 1500 мм.
7. Прибор М_01 мойка кухонная, М_02 посудомоечная машина взят из расстановки мебели (по шкафу с мойкой).
8. Стояки в коробах/шахтах не замоноличивать; стояк К1 в коробе — звукоизоляция стояка в коробе без жёсткого контакта с трубой; к арматуре и ревизиям — люк не меньше 300×400.

					Проект: Дом 331 м²	М 1:40
	Лист	№ док.	Подпись	Дата		
Дизайнер	Кырлан А.С.			04.11.26	План выводов сантехники · 1-й этаж	Стадия: П; Лист: 25; Листов: 168

Фрагмент 1. Санузел мастер (пом. 15)

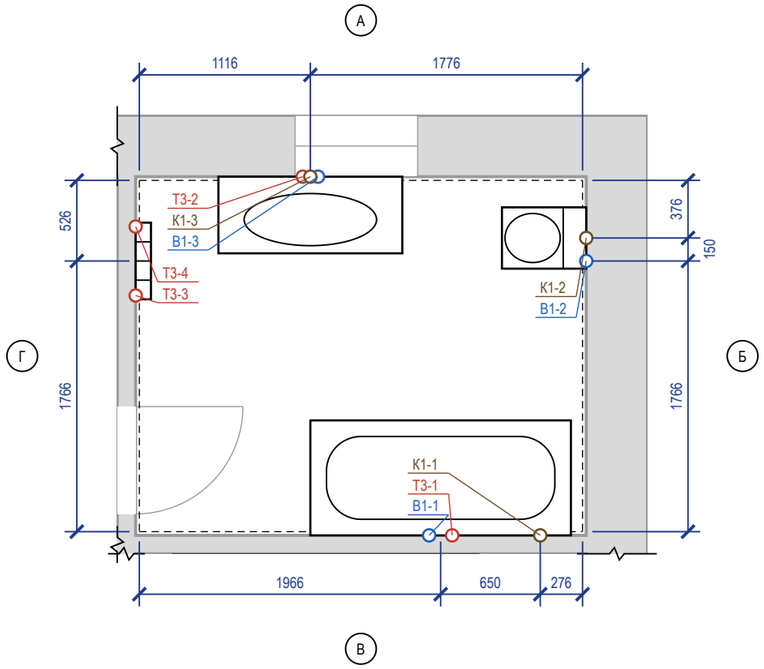

Фрагмент 2. Санузел 2 (пом. 20)

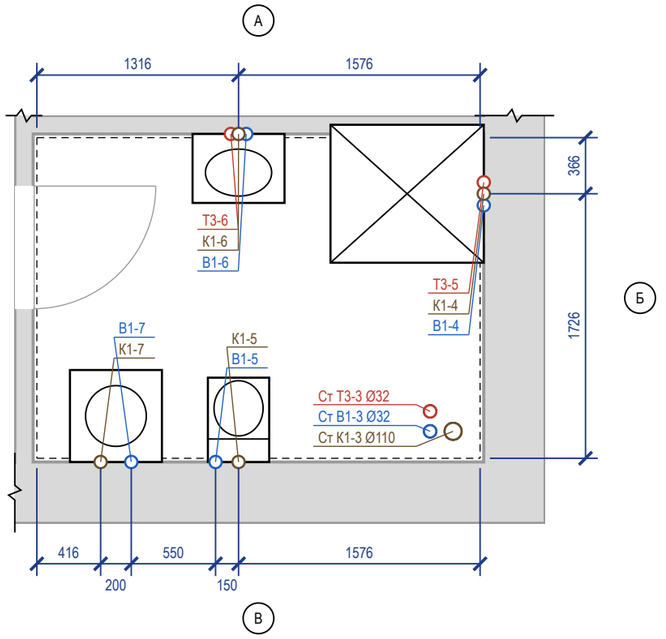

Ведомость привязок выводов

Код	Прибор	Ø	H, мм	Привязка от чист. стен, мм	Прим.
В1-1	С_05 ванна	½"	800	ст. В: 1001 от Б	межос. 150
Т3-1	С_05 ванна	½"	800	ст. В: 851 от Б	межос. 150
К1-1	С_05 ванна	Ø50	50	ст. В: 276 от Б	
В1-2	С_06 унитаз подвесной	½"	250	ст. Б: 526 от А	в раме инсталляции
К1-2	С_06 унитаз подвесной	Ø110	220	ст. Б: 376 от А	
В1-3	С_07 умывальник	½"	600	ст. А: 1166 от Г	межос. 100
Т3-2	С_07 умывальник	½"	600	ст. А: 1066 от Г	межос. 100
К1-3	С_07 умывальник	Ø50	500	ст. А: 1116 от Г	
Т3-3	С_08 полотенцесушитель	½"	1150	ст. Г: 751 от А	подача, межос. 450; байпас и краны
Т3-4	С_08 полотенцесушитель	½"	1150	ст. Г: 301 от А	обратка
В1-4	С_09 душ	½"	1200	ст. Б: 441 от А	межос. 150
Т3-5	С_09 душ	½"	1200	ст. Б: 291 от А	межос. 150
К1-4	С_09 душ	Ø50	70	ст. Б: 366 от А	сифон поддона
В1-5	С_10 унитаз подвесной	½"	250	ст. В: 1166 от Г	в раме инсталляции
К1-5	С_10 унитаз подвесной	Ø110	220	ст. В: 1316 от Г	
В1-6	С_11 умывальник	½"	600	ст. А: 1366 от Г	межос. 100
Т3-6	С_11 умывальник	½"	600	ст. А: 1266 от Г	межос. 100
К1-6	С_11 умывальник	Ø50	500	ст. А: 1316 от Г	
В1-7	ОБ_02 стиральная машина	½"	600	ст. В: 616 от Г	кран машины
К1-7	ОБ_02 стиральная машина	Ø50	600	ст. В: 416 от Г	

Условные обозначения


- вывод В1 (код — в ведомости привязок)
- вывод Т3 (код — в ведомости привязок)
- вывод К1 (код — в ведомости привязок)
- сантехприбор по расстановке (габарит модели)
- чистовая поверхность стены (от неё привязки)
- стояк «Ст К1-N / Ст В1-N» (ГОСТ 21.601), Ø мм
- линия обрыва (граница фрагмента)
- А — обозначение стены А–Г (как на развёртках)

Примечания


1. Привязки выводов даны от чистовых поверхностей стен (облицовка на сторону: санузел мастер — 24 мм (штукатурка 10 + клей 5 + плитка 9); санузел 2 24 мм (штукатурка 10 + клей 5 + плитка 9)); эти же грани — на развёртках и в раскладке плитки. Высоты — от чистого пола помещения.
2. До черновой разводки сверить по паспорту выбранного прибора (смеситель, инсталляция, сифон).
3. Горячая вода (Т3) — слева от холодной (В1), если смотреть на прибор. Допуск установки выводов: ±5 мм в группе, ±20 мм у отдельно стоящих.
4. Расчёт систем водоснабжения и канализации и подбор оборудования выполняет проектная организация; лист задаёт места и высоты выводов.
5. Стояки в коробах/шахтах не замоноличивать; стояк К1 в коробе — звукоизоляция стояка в коробе без жёсткого контакта с трубой; к арматуре и ревизиям — люк не меньше 300×400.

					Проект: Дом 331 м² — М 1:40
	Лист	№ док.	Подпись	Дата	
Дизайнер	Кырлан А.С.			04.11.26	План выводов сантехники · Мансарда
					Стадия: П; Лист: 26; Листов: 168


План этажа (М 1:400)

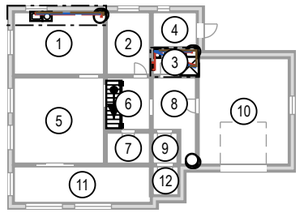

Фр. 1. Санузел 1 этажа (М 1:40)

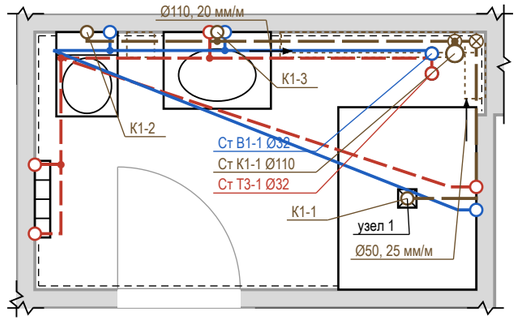


Узел 1. Душ без поддона, трап (С_01)

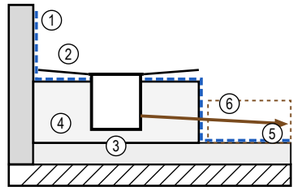

1. гидроизоляция 2 сл. на всю высоту стен душа, по всему санузлу; лента у фланца трапа и в углах
2. плитка, уклон 15 мм/м к трапу (СП 30.13330.2020, п. 17.9)
3. трап с фланцем под гидроизоляцию: монтажная высота 90 мм (до решётки) (принята, по паспорту модели)
4. подиум 100 мм у трапа, ступень 109 мм (ЦПС по гидроизоляции плиты) — предложение, согласовать с заказчиком
5. стяжка 35 мм
6. К1 Ø50, i = 25 мм/м, L = 1,70 м, Δh = 42 мм → Ст К1-1; за подиумом — короб 130×110

Пирог ≥ 132 мм = трап 90 + Δh 42 ≤ 35 + подиум 100 + плитка 14 мм

Фр. 2. Кухня-столовая (М 1:40)

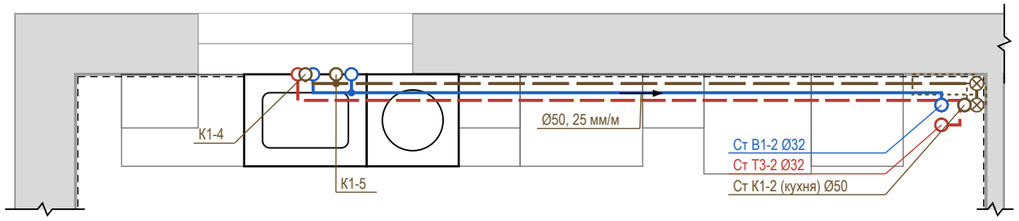

Условные обозначения


- В1 — водопровод хозяйственно-питьевой (ХВС), PP-R Ø20
- Т3 — горячее водоснабжение, подача (ГВС), PP-R Ø20
- К1 — канализация бытовая
- направление уклона К1 / пола: Ø, мм на 1 м
- ревизия (прочистка) К1 — доступ сохранить
- тройник (ответвление к прибору)
- короб К1 над чистым полом (ГКЛВ под плитку)
- вывод В1 (код — в ведомости привязок)
- вывод Т3 (код — в ведомости привязок)
- вывод К1 (код — в ведомости привязок)
- сантехприбор по расстановке (габарит модели)
- стояк «Ст К1-N / Ст В1-N» (ГОСТ 21.601), Ø мм
- линия обрыва (граница фрагмента)
- граница фрагмента на плане (Фр. N)

Профиль выпусков К1 (до врезки в стояк)

Выпуск	Прибор	Ø	L, м	i, мм/м	Δh, мм	Прокладка, мм
К1-2	С_02 унитаз подвесной	Ø110	2,54	20	51	короб 200×140
К1-4	М_01 мойка кухонная	Ø50	4,66	25	117	короб 200×110
К1-1	С_01 душ	Ø50	1,70	25	42	трап в подиуме 100 (35 + 100 + 14 ≥ 132), далее короб 130×110
К1-3	С_03 умывальник	Ø50	1,69	25	42	короб 130×110
К1-5	М_02 посудомоечная машина	Ø40	4,46	30	134	короб 210×110

Короб h×b: h — от чистого пола, b — от чистовой стены. Стяжка 35 мм — лист полов.

Узел ввода В1, Т3 (схема, без масштаба)

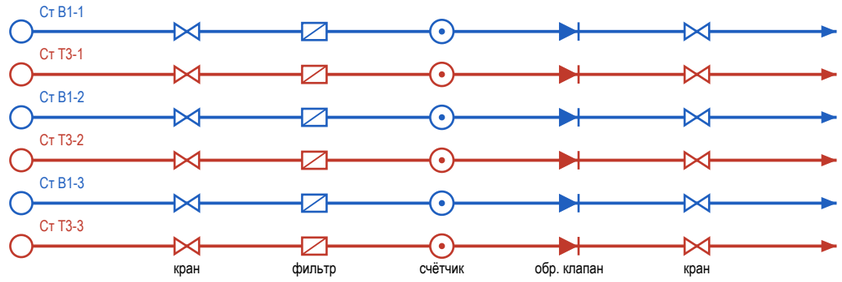

состав узла — по согласованию

⊗ Ст К1-1, Ст К1-2 (кухня), Ст К1-3: ревизия на стояке — люк в коробе


Примечания

1. Трассы принципиальные, построены от стояков вдоль стен помещений; фактическое положение фиксируется исполнительной схемой с привязками (фото с рулеткой) до закрытия.
2. Уклон К1 не менее 1/d и не более 150 мм/м (СП 30.13330.2020, п. 19.1), приняты практические уклоны; поворот — двумя отводами 45°, ревизия после поворота, доступ сохранить. Стояк К1 в коробе — звукоизоляция стояка в коробе, без жёсткого контакта короба с трубой.
3. Решение по К1: стяжка 35 мм не укрывает трубы (нужно Ø + Δh + 45 мм) — выпуски идут над чистым полом вдоль стен; К1-2, К1-4, К1-3, К1-5 — в коробе ГКЛВ под плитку (размеры в профиле). Короба — на развёртках; отметку низа врезки в стояк замерить до черновых работ.
4. К1-1 (С_01 душ, трап): монтажная высота трапа 90 до верха решётки (по паспорту) + уклон 42 = 132 мм ≤ стяжка 35 + подиум 100 + облицовка 14 мм трап в подиуме душевой зоны (узел 1 на этом листе), за краем подиума отвод — в коробе ГКЛВ 130×110 вдоль стены; подиум — предложение, согласовать с заказчиком.
5. Отводы К1-4 (4,7 м), К1-5 (4,5 м) длиннее 4 м без вентиляции — у прибора воздушный клапан Ø50 в доступном месте (за люком или в тумбе) либо вентилируемый отвод (EN 12056-2, табл. 4), подбор — проектная организация.
6. Состав узла ввода В1, Т3 — по согласованию: на схеме типовой узел — кран шаровой, фильтр, счётчик, обратный клапан, кран; состав и места не определены (записи реестра нет). Доступ к арматуре — через люк не меньше 300×400. Водопровод — в штробе стен или в коробах; трубы испытать давлением до закрытия (акт скрытых работ).
7. Расчёт систем, диаметры магистралей и подбор оборудования выполняет проектная организация; положение стояков, выпуск из дома и вентиляция стояков по проекту ВК дома, при его отсутствии — решение владельца с проектной организацией. Арматуру и привязки сверить по паспортам приборов.


					Проект: Дом 331 м²
	Лист	№ док.	Подпись	Дата	Схема разводки водопровода и канализации · 1-й этаж
Дизайнер	Кырлан А.С.			04.11.26	

Стадия	Лист	Листов
П	27	168


План этажа (М 1:200)

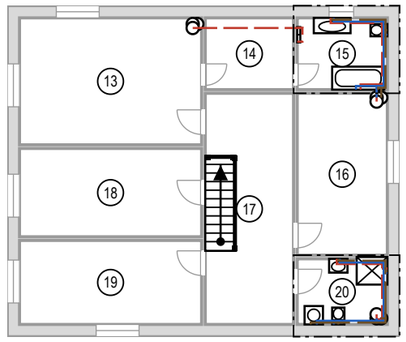

Фр. 1. Санузел мастер (М 1:40)

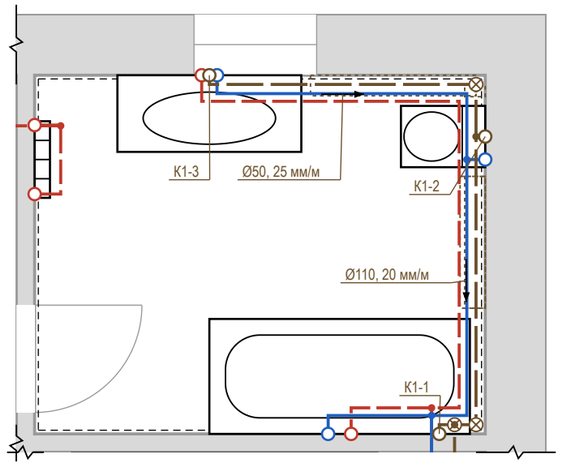

Фр. 2. Санузел 2 (М 1:40)

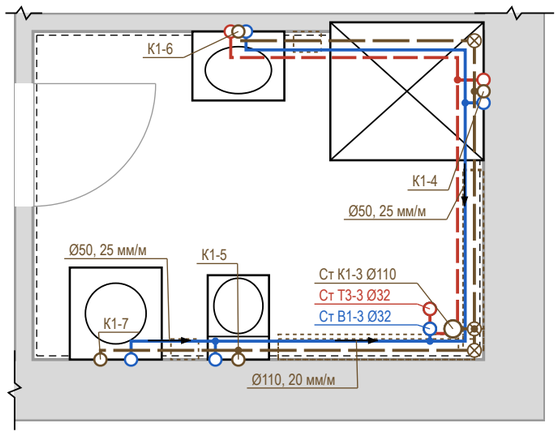

Условные обозначения


- В1 — водопровод хозяйственно-питьевой (ХВС), PP-R Ø20
- Т3 — горячее водоснабжение, подача (ГВС), PP-R Ø20
- К1 — канализация бытовая
- направление уклона К1 / пола: Ø, мм на 1 м
- ревизия (прочистка) К1 — доступ сохранить
- тройник (ответвление к прибору)
- короб К1 над чистым полом (ГКЛВ под плитку)
- вывод В1 (код — в ведомости привязок)
- вывод Т3 (код — в ведомости привязок)
- вывод К1 (код — в ведомости привязок)
- сантехприбор по расстановке (габарит модели)
- стояк «Ст К1-N / Ст В1-N» (ГОСТ 21.601), Ø мм
- линия обрыва (граница фрагмента)
- граница фрагмента на плане (Фр. N)

Профиль выпусков К1 (до врезки в стояк)

Выпуск	Прибор	Ø	L, м	i, мм/м	Δh, мм	Прокладка, мм
К1-2	С_06 унитаз подвесной	Ø110	2,40	20	48	короб 190×140
К1-5	С_10 унитаз подвесной	Ø110	1,88	20	38	короб 180×140
К1-3	С_07 умывальник	Ø50	4,48	25	112	короб 200×110
К1-6	С_11 умывальник	Ø50	3,62	25	91	короб 180×110
К1-7	ОБ_02 стиральная машина	Ø50	2,78	25	70	короб 150×110
К1-4	С_09 душ	Ø50	1,75	25	44	короб 130×110
К1-1	С_05 ванна	Ø50	0,48	25	12	над полом за приборами

Короб h×b: h — от чистого пола, b — от чистовой стены. Стяжка 35 мм — лист полов.

Узел ввода В1, Т3 (схема, без масштаба)

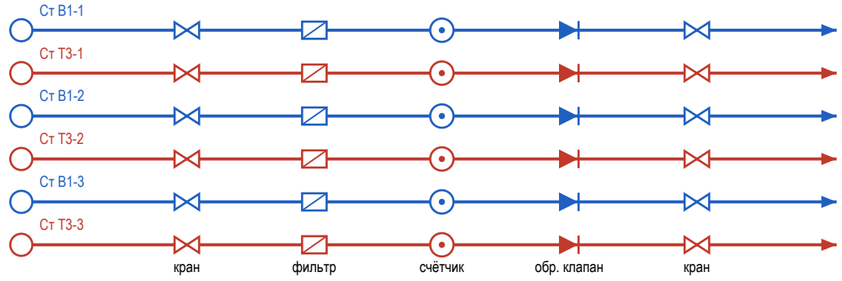

состав узла — по согласованию


⊗ Ст К1-1, Ст К1-2 (кухня), Ст К1-3: ревизия на стояке — люк в коробе


Примечания

1. Трассы принципиальные, построены от стояков вдоль стен помещений; фактическое положение фиксируется исполнительной схемой с привязками (фото с рулеткой) до закрытия.
2. Уклон К1 не менее 1/d и не более 150 мм/м (СП 30.13330.2020, п. 19.1), приняты практические уклоны; поворот — двумя отводами 45°, ревизия после поворота, доступ сохранить. Стояк К1 в коробе — звукоизоляция стояка в коробе, без жёсткого контакта короба с трубой.
3. Решение по К1: стяжка 35 мм не укрывает трубы (нужно Ø + Δh + 45 мм) — выпуски идут над чистым полом вдоль стен: К1-1 — за приборами и в раме инсталляции; К1-2, К1-5, К1-3, К1-6, К1-7, К1-4 — в коробе ГКЛВ под плитку (размеры в профиле). Короба — на развёртках; отметку низа врезки в стояк замерить до черновых работ.
4. Отводы К1-3 (4,5 м) длиннее 4 м без вентиляции — у прибора воздушный клапан Ø50 в доступном месте (за люком или в тумбе) либо вентилируемый отвод (EN 12056-2, табл. 4), подбор — проектная организация.
5. Состав узла ввода В1, Т3 — по согласованию: на схеме типовой узел — кран шаровой, фильтр, счётчик, обратный клапан, кран; состав и места не определены (записи реестра нет). Доступ к арматуре — через люк не меньше 300×400. Водопровод — в штробе стен или в коробах; трубы испытать давлением до закрытия (акт скрытых работ).
6. Расчёт систем, диаметры магистралей и подбор оборудования выполняет проектная организация; положение стояков, выпуск из дома и вентиляция стояков по проекту ВК дома, при его отсутствии — решение владельца с проектной организацией. Арматуру и привязки сверить по паспортам приборов.

					Проект: Дом 331 м²
	Лист	№ док.	Подпись	Дата	
Дизайнер	Кырлан А.С.			04.11.26	Схема разводки водопровода и канализации · Мансарда
					Стадия: П; Лист: 28; Листов: 168

Схема В1 (М 1:50; по вертикали и горизонтали один масштаб, глубина — ×0,5 под 45°)

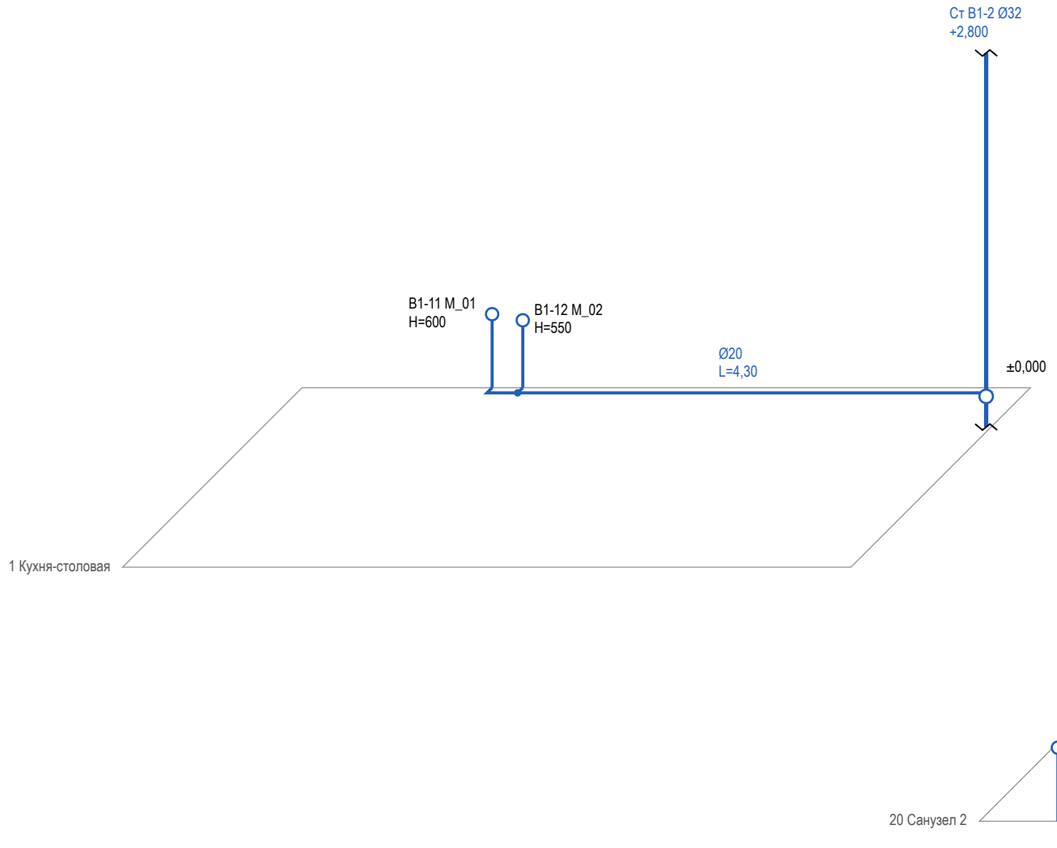

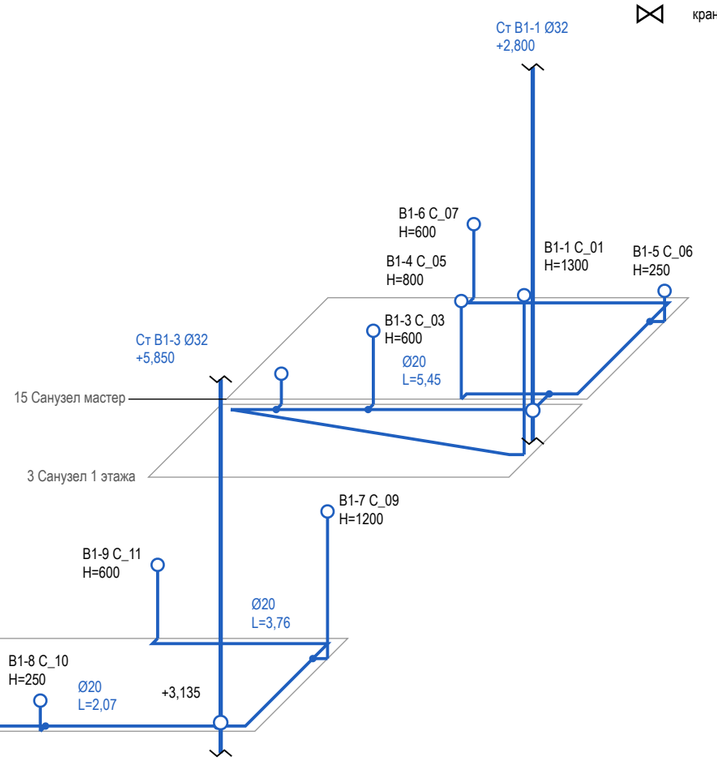

Условные обозначения

- B1 — водопровод хозяйственно-питьевой (ХВС), PP-R Ø20
- вывод В1 (код — в ведомости привязок)
- стояк «Ст К1-N / Ст В1-N» (ГОСТ 21.601), Ø мм
- стояк в плане (на отметке пола); вертикаль — стояк по высоте, разрыв — перекрытие
- тройник (ответвление к прибору)
- кран шаровой

Примечания


1. Схема В1 построена по тем же трассам, что план разводки: положение в плане сохранено, глубина — в масштабе ×0,5. Трассы принципиальные; фактическое положение фиксируется исполнительной схемой до закрытия.
2. Высоты Н — от чистого пола помещения, мм. Отметка прокладки магистрали В1 (в стяжке, в стене или по полу) в данных не задана: участки показаны на уровне пола условно (записи реестра нет).
3. Узел ввода В1 (кран, фильтр, счётчик, обратный клапан, кран) — на схеме разводки; состав узла ввода — по согласованию. Кран шаровой — на первом участке от стояка.
4. Трубы испытать давлением до закрытия (акт скрытых работ, опрессовка по СП 73.13330.2016).
5. Диаметры, высоты выводов и места кранов — по паспортам выбранных приборов и расчёту проектной организации.
6. Расчёт систем, диаметры магистралей и подбор оборудования выполняет проектная организация.

					Проект: Дом 331 м²	М 1:50
	Лист	№ док.	Подпись	Дата	Аксонометрическая схема В1 (холодное водоснабжение)	Стадия / Лист / Листов
Дизайнер	Кырлан А.С.			04.11.26		П / 29 / 168

Схема Т3 (М 1:50; по вертикали и горизонтали один масштаб, глубина — ×0,5 под 45°)

Условные обозначения

- Т3 — горячее водоснабжение, подача (ГВС), PP-R Ø20
- вывод Т3 (код — в ведомости привязок)
- стояк «Ст К1-N / Ст В1-N» (ГОСТ 21.601), Ø мм
- стояк в плане (на отметке пола); вертикаль — стояк по высоте, разрыв — перекрытие
- тройник (ответвление к прибору)
- кран шаровой

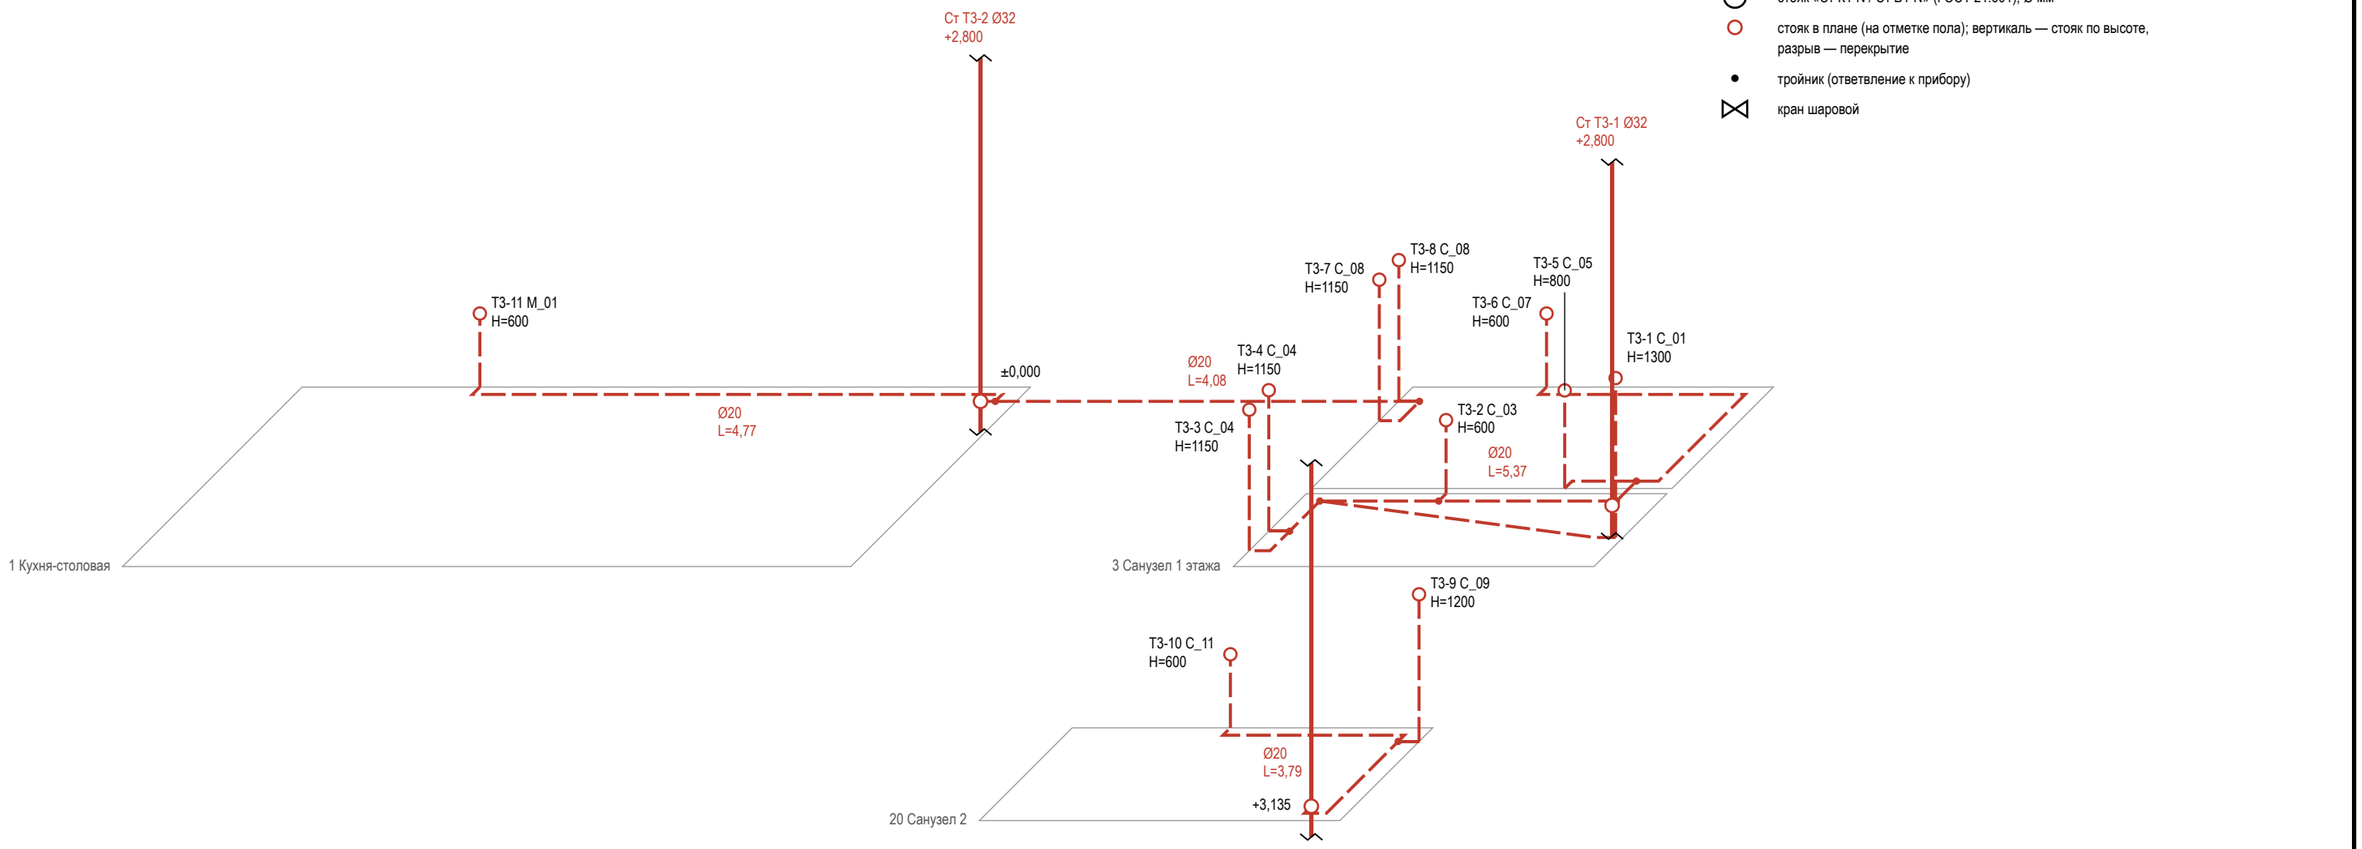

Примечания

1. Схема Т3 построена по тем же трассам, что план разводки: положение в плане сохранено, глубина — в масштабе ×0,5. Трассы принципиальные; фактическое положение фиксируется исполнительной схемой до закрытия.
2. Высоты Н — от чистого пола помещения, мм. Отметка прокладки магистрали Т3 (в стяжке, в стене или по полу) в данных не задана: участки показаны на уровне пола условно (записи реестра нет).
3. Узел ввода Т3 (кран, фильтр, счётчик, обратный клапан, кран) — на схеме разводки; состав узла ввода — по согласованию. Кран шаровой — на первом участке от стояка.
4. Циркуляция ГВС в данных не задана — циркуляционного трубопровода на схеме нет (записи реестра нет).
5. Трубы испытать давлением до закрытия (акт скрытых работ, опрессовка по СП 73.13330.2016).
6. Диаметры, высоты выводов и места кранов — по паспортам выбранных приборов и расчёту проектной организации.
7. Расчёт систем, диаметры магистралей и подбор оборудования выполняет проектная организация.


	Лист	№ док.	Подпись	Дата
Дизайнер	Кырлан А.С.			04.11.26

Проект: Дом 331 м² — **М 1:50**

Аксонометрическая схема Т3 (горячее водоснабжение)

Стадия	Лист	Листов
П	30	168

Схема К1 (М 1:50; по вертикали и горизонтали один масштаб, глубина — ×0,5 под 45°)

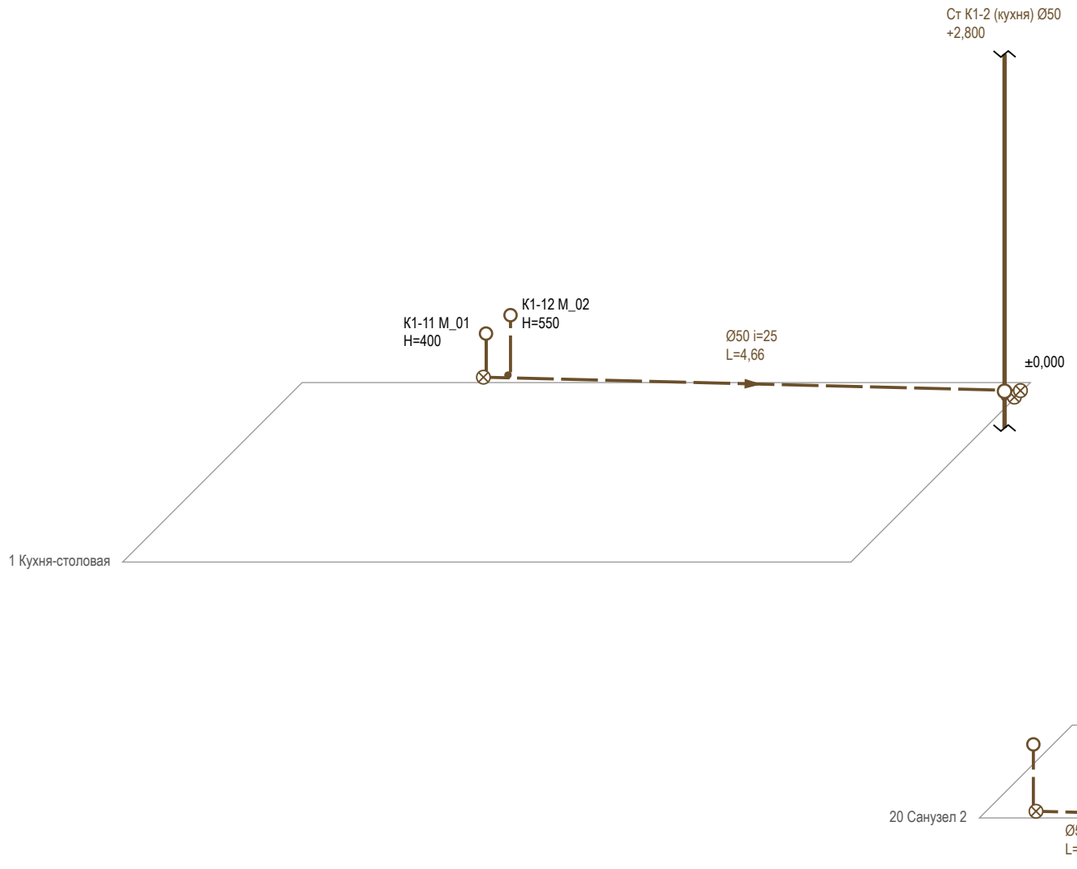

Условные обозначения


- К1 — канализация бытовая
- вывод К1 (код — в ведомости привязок)
- стояк «Ст К1-N / Ст В1-N» (ГОСТ 21.601), Ø мм
- стояк в плане (на отметке пола); вертикаль — стояк по высоте, разрыв — перекрытие
- направление уклона К1 / пола: Ø, мм на 1 м
- ревизия (прочистка) К1 — доступ сохранить
- тройник (ответвление к прибору)

Примечания

1. Схема К1 построена по тем же трассам, что план разводки: положение в плане сохранено, глубина — в масштабе ×0,5. Трассы принципиальные; фактическое положение фиксируется исполнительной схемой до закрытия.
2. Отметки — от плиты перекрытия: низ трубы у врезки в стояк — отметка из данных выпуска, к прибору труба поднимается на уклон i, мм/м (уклон не менее 1/d и не более 150 мм/м, СП 30.13330.2020, п. 19.1); чистый пол — выше плиты на стяжку (высота пирога пола). Высота выпуска прибора H — от чистого пола.
3. Ревизия — на повороте и в начале участка; стояк К1 в коробе с люком — звукоизоляция стояка в коробе; поворот — двумя отводами 45°.
4. Трубы испытать давлением до закрытия (акт скрытых работ, опрессовка по СП 73.13330.2016).
5. Диаметры, высоты выводов и места кранов — по паспортам выбранных приборов и расчёту проектной организации.
6. Расчёт систем, диаметры магистралей и подбор оборудования выполняет проектная организация.

					Проект: Дом 331 м²	М 1:50
	Лист	№ док.	Подпись	Дата		
Дизайнер	Кырлан А.С.			04.11.26	Аксонометрическая схема К1 (канализация)	Стадия: П; Лист: 31; Листов: 168

Стена А (М 1:20)

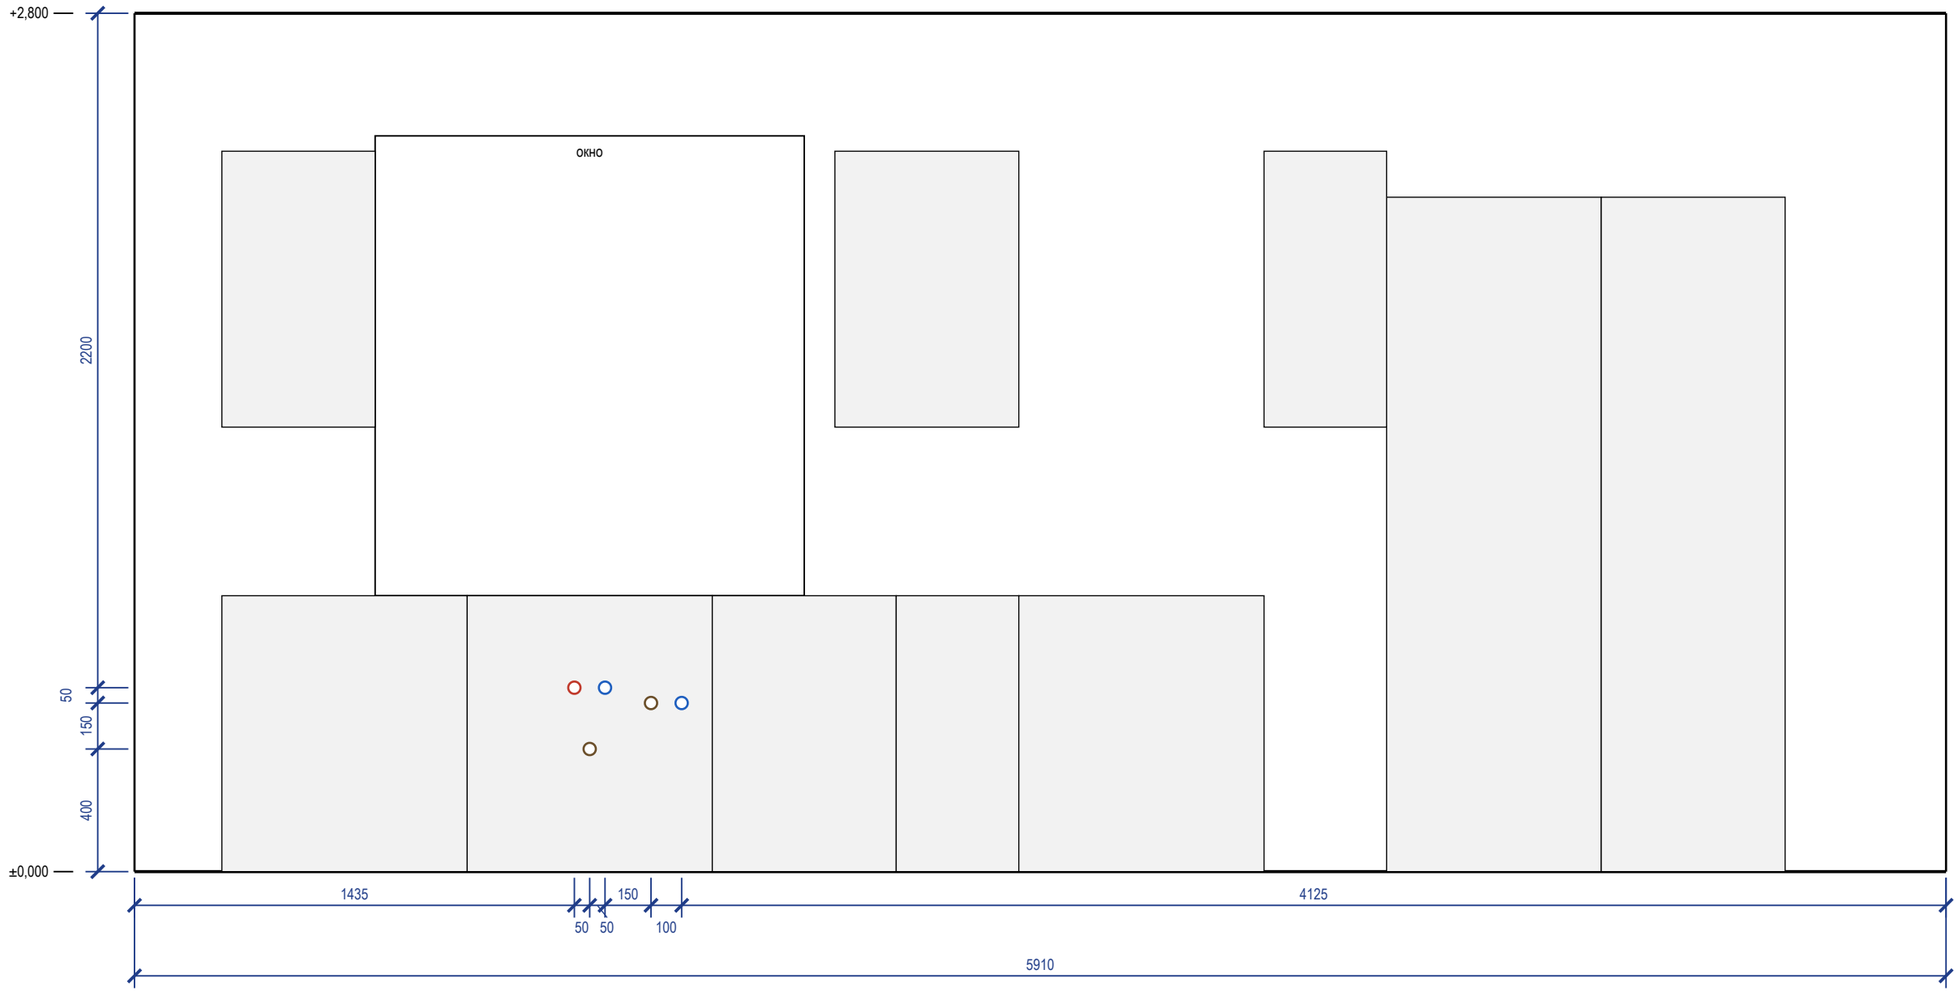

Ведомость привязок выводов (от чистого пола и угла)

Код	Прибор	Ø	H, мм	Привязка, мм
В1-11	М_01 мойка кухонная	½"	600	ст. А: 1535 от лев. угла
Т3-11	М_01 мойка кухонная	½"	600	ст. А: 1435 от лев. угла
К1-11	М_01 мойка кухонная	Ø50	400	ст. А: 1485 от лев. угла
В1-12	М_02 посудомоечная машина	½"	550	ст. А: 1785 от лев. угла
К1-12	М_02 посудомоечная машина	Ø40	550	ст. А: 1685 от лев. угла

Условные обозначения


- вывод В1 (код — в ведомости привязок)
- вывод Т3 (код — в ведомости привязок)
- вывод К1 (код — в ведомости привязок)
- сантехприбор по расстановке (габарит модели)
- дверной проём; окно — сплошной контур

Примечания


1. Габариты и высоты приборов, межосевые смесителей и места кранов — по паспортам выбранных приборов, сверяются до разметки стен.
2. Высоты H — от чистого пола помещения, мм; отметка чистого пола и потолка — у левого края вида (от ±0,000 объекта). Привязки — от левого чистового угла вида (облицовка стен вычтена), как на развёртках стен.
3. Стояки в помещении: Ст К1-2 (кухня) Ø50, Ст В1-2 Ø32, Ст Т3-2 Ø32 — положение на плане выводов; выводы подключаются к ним по схеме разводки.
4. Ревизионные люки к арматуре и ревизиям в данных не заданы: место и размер не определены (записи реестра нет).
5. Мойка, ПММ и фильтр — выводы в шкафу мойки; диаметры и положение сифона и кранов сверить по паспортам приборов и чертежам модуля.
6. Часть подписей выводов не уместилась у знака: коды и высоты — в ведомости привязок.
7. Расчёт систем водоснабжения и канализации и подбор оборудования выполняет проектная организация; лист задаёт места и высоты выводов.

					Проект: Дом 331 м²	М 1:20
	Лист	№ док.	Подпись	Дата	Развёртки мокрых зон: выводы ВК. Кухня-столовая	Стадия / Лист / Листов
Дизайнер	Кырлан А.С.			04.11.26		П / 32 / 168

Стена А (М 1:20)

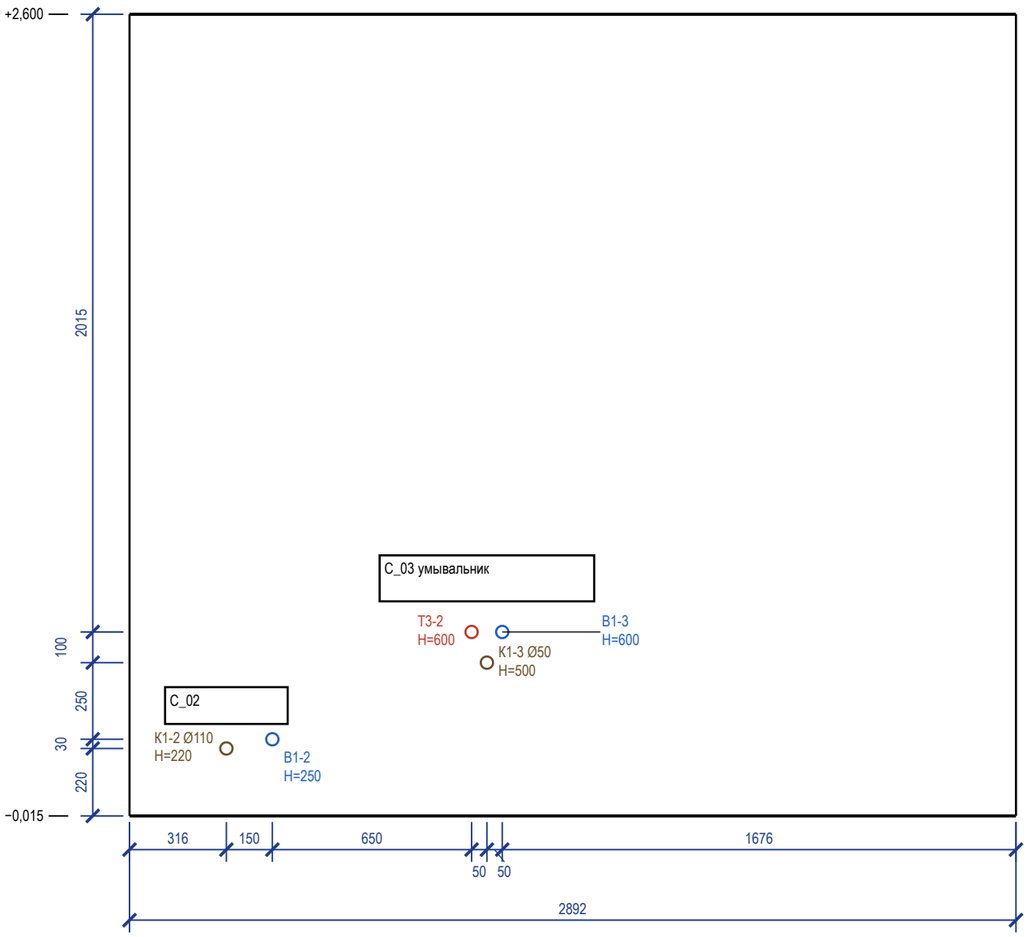

Стена Б (М 1:20)

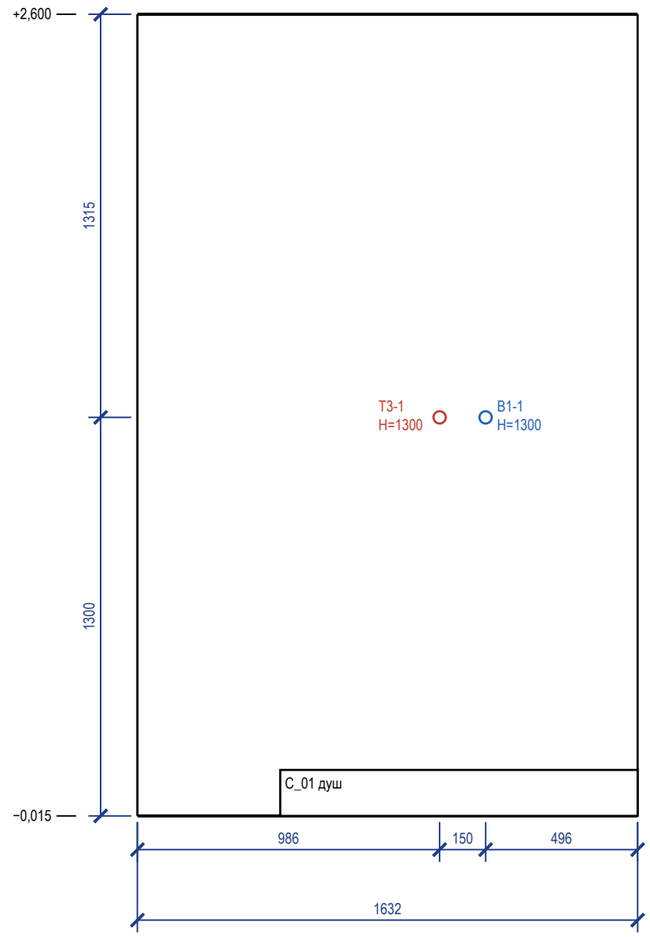

Ведомость привязок выводов (от чистого пола и угла)

Код	Прибор	Ø	H, мм	Привязка, мм
B1-2	C_02 унитаз подвесной	½"	250	ст. А: 466 от лев. угла
K1-2	C_02 унитаз подвесной	Ø110	220	ст. А: 316 от лев. угла
B1-3	C_03 умывальник	½"	600	ст. А: 1216 от лев. угла
T3-2	C_03 умывальник	½"	600	ст. А: 1116 от лев. угла

Ведомость привязок (продолжение)

Код	Прибор	Ø	H, мм	Привязка, мм
K1-3	C_03 умывальник	Ø50	500	ст. А: 1166 от лев. угла
B1-1	C_01 душ	½"	1300	ст. Б: 1136 от лев. угла
T3-1	C_01 душ	½"	1300	ст. Б: 986 от лев. угла

Условные обозначения


- вывод B1 (код — в ведомости привязок)
- вывод T3 (код — в ведомости привязок)
- вывод K1 (код — в ведомости привязок)
- сантехприбор по расстановке (габарит модели)
- дверной проём; окно — сплошной контур

Примечания


1. Габариты и высоты приборов, межосевые смесителей и места кранов — по паспортам выбранных приборов, сверяются до разметки стен.
2. Высоты H — от чистого пола помещения, мм; отметка чистого пола и потолка — у левого края вида (от ±0,000 объекта). Привязки — от левого чистового угла вида (облицовка стен вычтена), как на развёртках стен.
3. Выводы в полу (K1-1): трап, лоток, выпуск отдельностоящей ванны, подвод к стойке напольного смесителя — на развёртке их нет; место и пирог пола лист «Схема разводки» (профиль K1, узел 1).
4. Стояки в помещении: Ст K1-1 Ø110, Ст B1-1 Ø32, Ст T3-1 Ø32 — положение на плане выводов; выводы подключаются к ним по схеме разводки.
5. Ревизионные люки к арматуре и ревизиям в данных не заданы: место и размер не определены (записи реестра нет).
6. Помещение «Санузел 1 этажа» — 2 листа: стены 1) А, Б; 2) В, Г.
7. Расчёт систем водоснабжения и канализации и подбор оборудования выполняет проектная организация; лист задаёт места и высоты выводов.

					Проект: Дом 331 м²	М 1:20
	Лист	№ док.	Подпись	Дата	Развёртки мокрых зон: выводы ВК. Санузел 1 этажа (лист 1 из 2)	Стадия / Лист / Листов
Дизайнер	Кырлан А.С.			04.11.26		П / 33 / 168

Стена В (М 1:20)

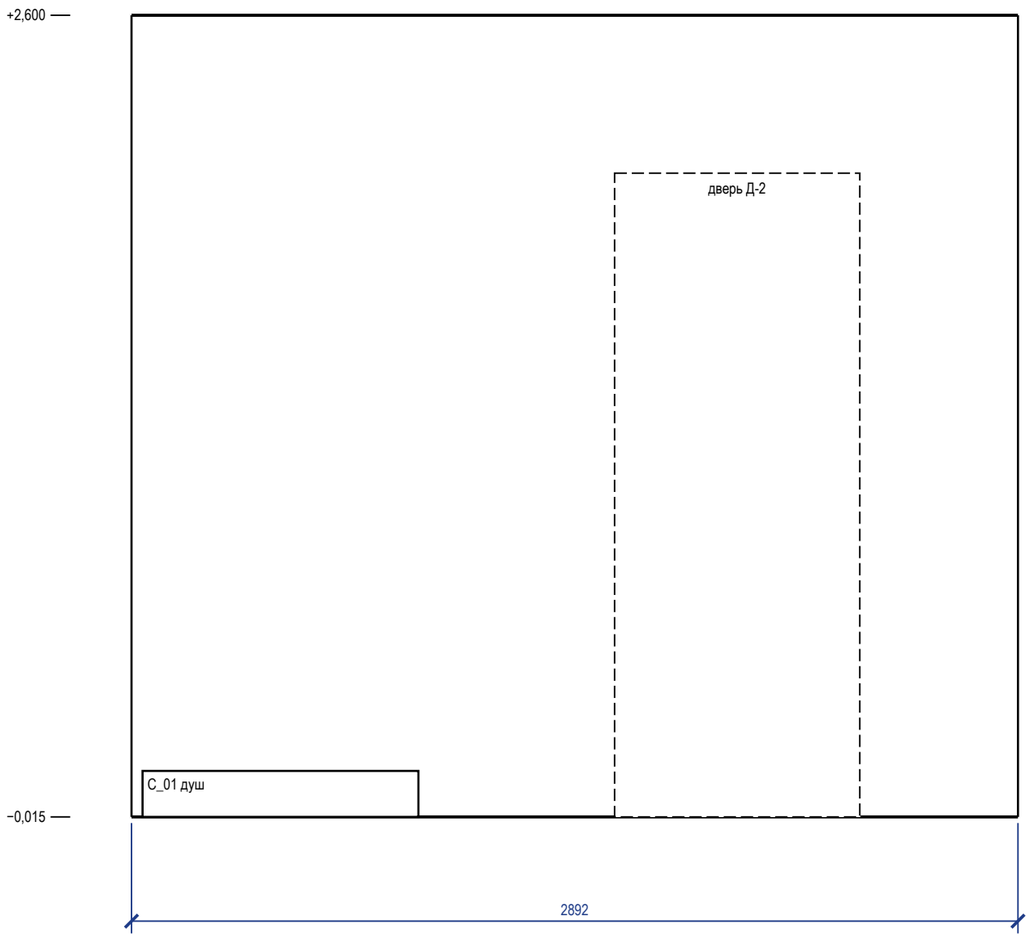

Стена Г (М 1:20)

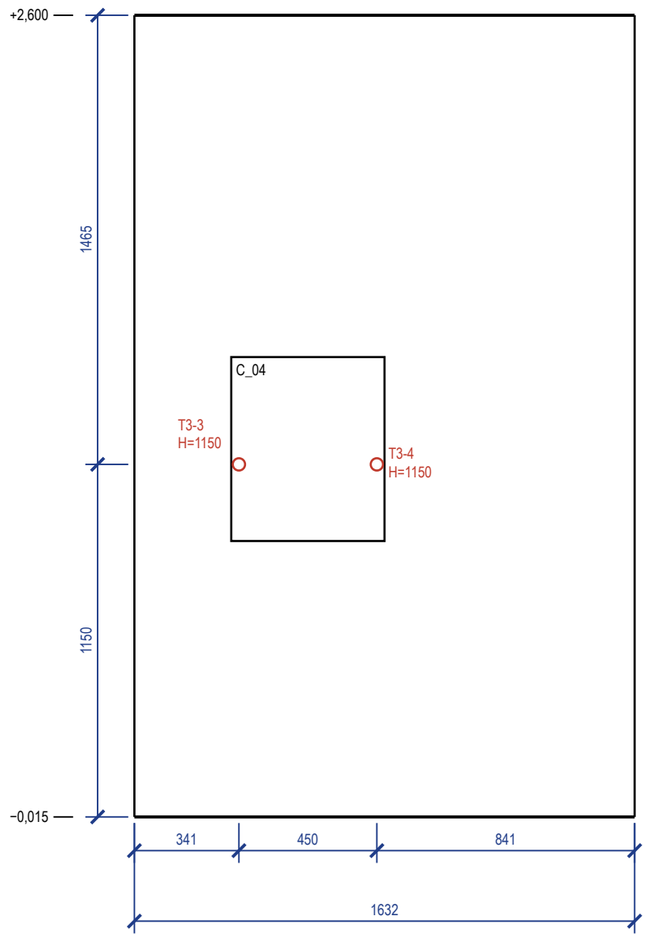

Ведомость привязок выводов (от чистого пола и угла)

Код	Прибор	Ø	H, мм	Привязка, мм
Т3-3	С_04 полотенцесушитель	½"	1150	ст. Г: 341 от лев. угла
Т3-4	С_04 полотенцесушитель	½"	1150	ст. Г: 791 от лев. угла

Условные обозначения

- вывод В1 (код — в ведомости привязок)
- вывод Т3 (код — в ведомости привязок)
- вывод К1 (код — в ведомости привязок)
- сантехприбор по расстановке (габарит модели)
- дверной проём; окно — сплошной контур

Примечания

1. Габариты и высоты приборов, межосевые смесителей и места кранов — по паспортам выбранных приборов, сверяются до разметки стен.
2. Высоты H — от чистого пола помещения, мм; отметка чистого пола и потолка — у левого края вида (от ±0,000 объекта). Привязки — от левого чистового угла вида (облицовка стен вычтена), как на развёртках стен.
3. Выводы в полу (К1-1): трап, лоток, выпуск отдельностоящей ванны, подвод к стойке напольного смесителя — на развёртке их нет; место и пирог пола лист «Схема разводки» (профиль К1, узел 1).
4. Стояки в помещении: Ст К1-1 Ø110, Ст В1-1 Ø32, Ст Т3-1 Ø32 — положение на плане выводов; выводы подключаются к ним по схеме разводки.
5. Ревизионные люки к арматуре и ревизиям в данных не заданы: место и размер не определены (записи реестра нет).
6. Помещение «Санузел 1 этажа» — 2 листа: стены 1) А, Б; 2) В, Г.
7. Расчёт систем водоснабжения и канализации и подбор оборудования выполняет проектная организация; лист задаёт места и высоты выводов.


	Лист	№ док.	Подпись	Дата
Дизайнер	Кырлан А.С.			04.11.26

Проект: Дом 331 м² — М 1:20


Развёртки мокрых зон: выводы ВК. Санузел 1 этажа (лист 2 из 2)

Стадия	Лист	Листов
П	34	168

Стена А (М 1:20)

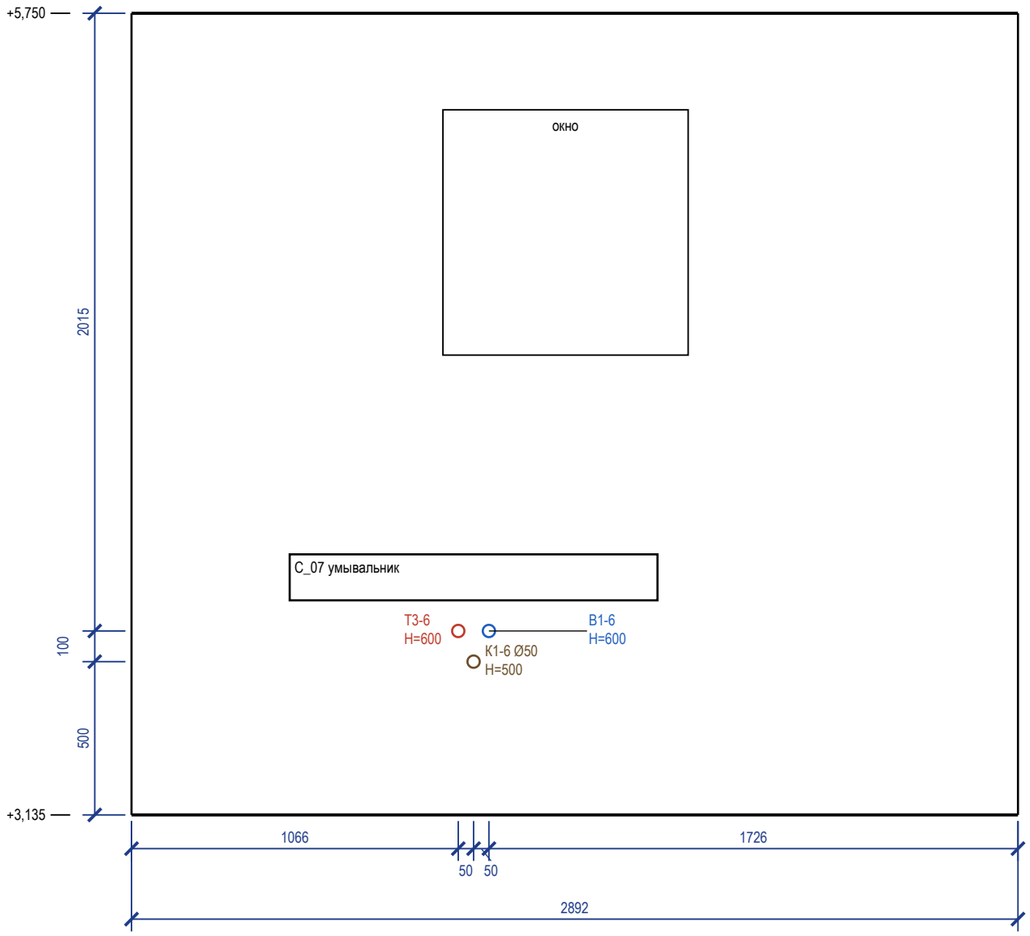

Стена Б (М 1:20)

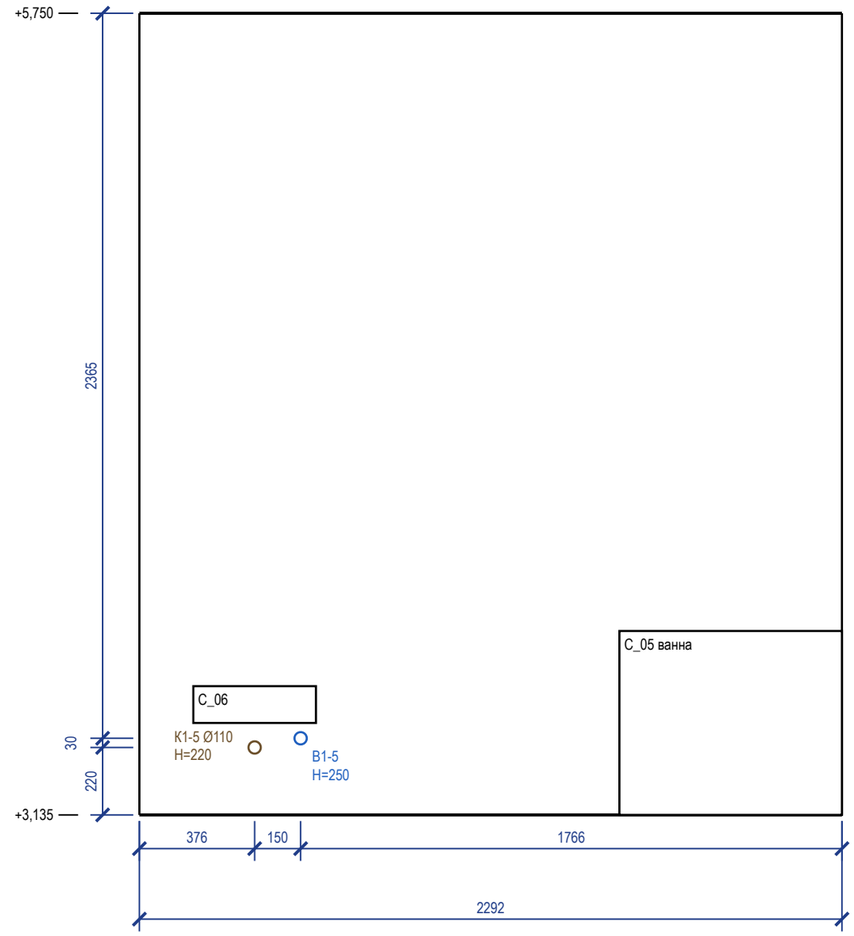

Ведомость привязок выводов (от чистого пола и угла)

Код	Прибор	Ø	H, мм	Привязка, мм
B1-6	C_07 умывальник	½"	600	ст. А: 1166 от лев. угла
T3-6	C_07 умывальник	½"	600	ст. А: 1066 от лев. угла
K1-6	C_07 умывальник	Ø50	500	ст. А: 1116 от лев. угла
B1-5	C_06 унитаз подвесной	½"	250	ст. Б: 526 от лев. угла
K1-5	C_06 унитаз подвесной	Ø110	220	ст. Б: 376 от лев. угла

Условные обозначения


- вывод B1 (код — в ведомости привязок)
- вывод T3 (код — в ведомости привязок)
- вывод K1 (код — в ведомости привязок)
- сантехприбор по расстановке (габарит модели)
- дверной проём; окно — сплошной контур

Примечания


1. Габариты и высоты приборов, межосевые смесителей и места кранов — по паспортам выбранных приборов, сверяются до разметки стен.
2. Высоты H — от чистого пола помещения, мм; отметка чистого пола и потолка — у левого края вида (от ±0,000 объекта). Привязки — от левого чистового угла вида (облицовка стен вычтена), как на развёртках стен.
3. Ревизионные люки к арматуре и ревизиям в данных не заданы: место и размер не определены (записи реестра нет).
4. Помещение «Санузел мастер» — 2 листа: стены 1) А, Б; 2) В, Г.
5. Расчёт систем водоснабжения и канализации и подбор оборудования выполняет проектная организация; лист задаёт места и высоты выводов.

					Проект: Дом 331 м²	М 1:20
	Лист	№ док.	Подпись	Дата	Развёртки мокрых зон: выводы ВК. Санузел мастер (лист 1 из 2)	Стадия / Лист / Листов
Дизайнер	Кырлан А.С.			04.11.26		П / 35 / 168

Стена В (М 1:20)

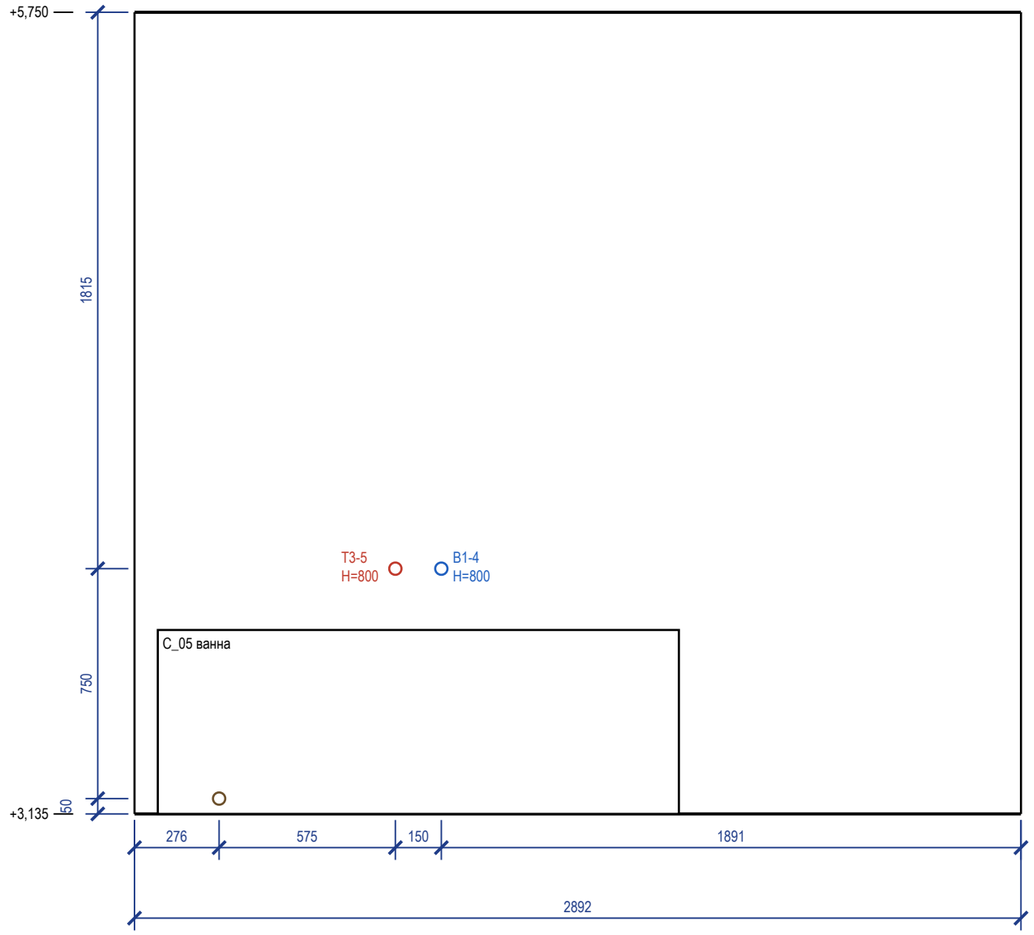

Стена Г (М 1:20)

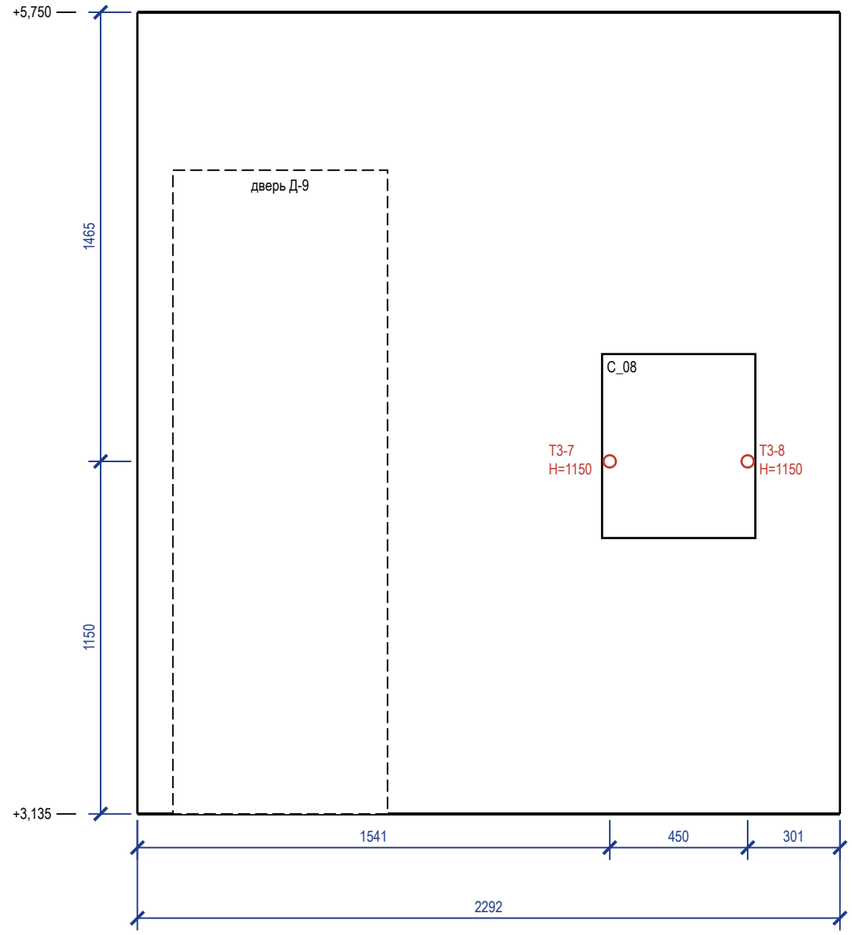

Ведомость привязок выводов (от чистого пола и угла)

Код	Прибор	Ø	H, мм	Привязка, мм
В1-4	С_05 ванна	½"	800	ст. В: 1001 от лев. угла
Т3-5	С_05 ванна	½"	800	ст. В: 851 от лев. угла
К1-4	С_05 ванна	Ø50	50	ст. В: 276 от лев. угла
Т3-7	С_08 полотенцесушитель	½"	1150	ст. Г: 1541 от лев. угла
Т3-8	С_08 полотенцесушитель	½"	1150	ст. Г: 1991 от лев. угла

Условные обозначения

- вывод В1 (код — в ведомости привязок)
- вывод Т3 (код — в ведомости привязок)
- вывод К1 (код — в ведомости привязок)
- сантехприбор по расстановке (габарит модели)
- дверной проём; окно — сплошной контур

Примечания

1. Габариты и высоты приборов, межосевые смесителей и места кранов — по паспортам выбранных приборов, сверяются до разметки стен.
2. Высоты Н — от чистого пола помещения, мм; отметка чистого пола и потолка — у левого края вида (от ±0,000 объекта). Привязки — от левого чистового угла вида (облицовка стен вычтена), как на развёртках стен.
3. Ревизионные люки к арматуре и ревизиям в данных не заданы: место и размер не определены (записи реестра нет).
4. Часть подписей выводов не уместилась у знака: коды и высоты — в ведомости привязок.
5. Помещение «Санузел мастер» — 2 листа: стены 1) А, Б; 2) В, Г.
6. Расчёт систем водоснабжения и канализации и подбор оборудования выполняет проектная организация; лист задаёт места и высоты выводов.


	Лист	№ док.	Подпись	Дата
Дизайнер	Кырлан А.С.			04.11.26

Проект: Дом 331 м² — **М 1:20**


Развёртки мокрых зон: выводы ВК. Санузел мастер (лист 2 из 2)

Стадия	Лист	Листов
П	36	168

Стена А (М 1:20)

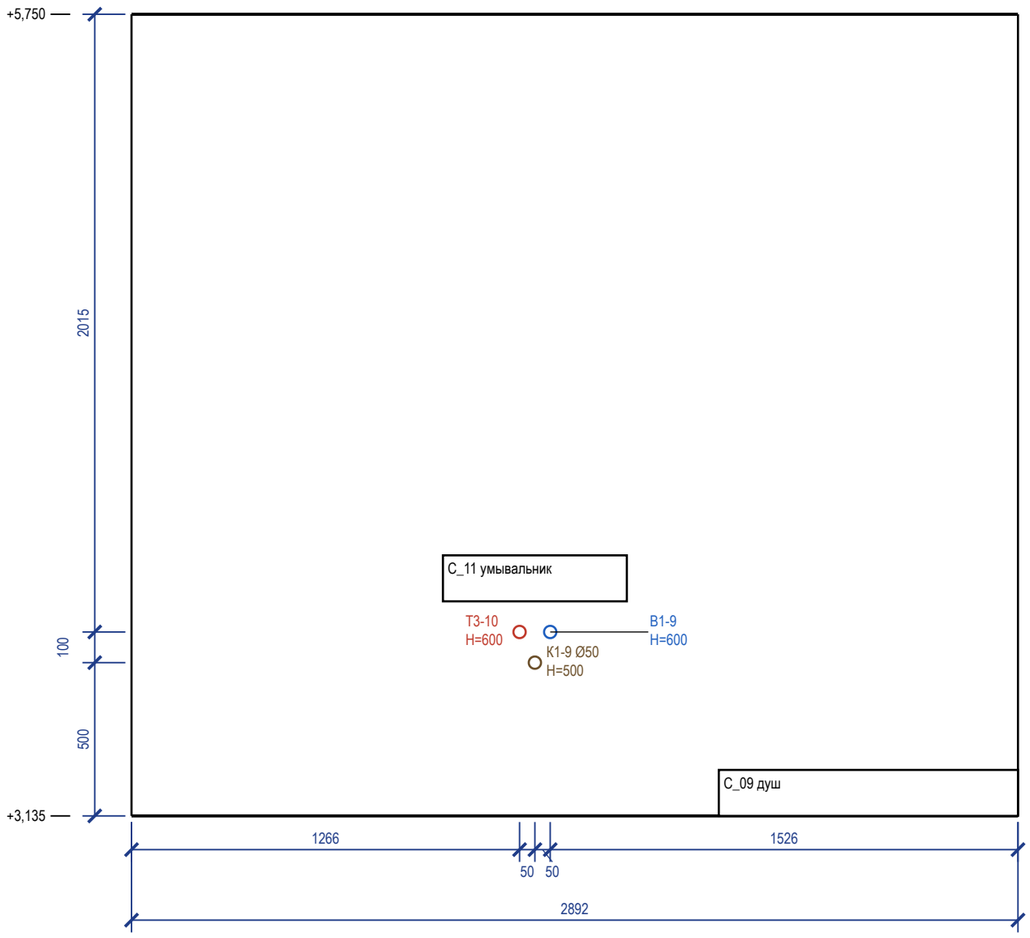

Стена Б (М 1:20)

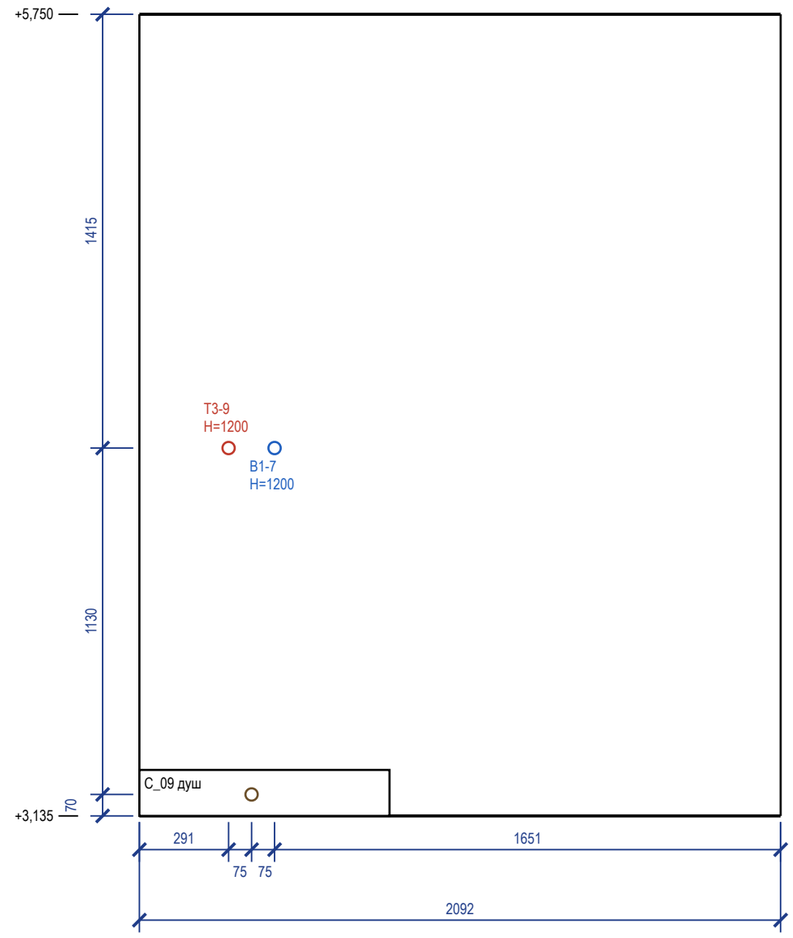

Ведомость привязок выводов (от чистого пола и угла)

Код	Прибор	Ø	H, мм	Привязка, мм
B1-9	C_11 умывальник	½"	600	ст. А: 1366 от лев. угла
T3-10	C_11 умывальник	½"	600	ст. А: 1266 от лев. угла
K1-9	C_11 умывальник	Ø50	500	ст. А: 1316 от лев. угла
B1-7	C_09 душ	½"	1200	ст. Б: 441 от лев. угла
T3-9	C_09 душ	½"	1200	ст. Б: 291 от лев. угла
K1-7	C_09 душ	Ø50	70	ст. Б: 366 от лев. угла

Условные обозначения

- вывод B1 (код — в ведомости привязок)
- вывод T3 (код — в ведомости привязок)
- вывод K1 (код — в ведомости привязок)
- сантехприбор по расстановке (габарит модели)
- дверной проём; окно — сплошной контур

Примечания

1. Габариты и высоты приборов, межосевые смесителей и места кранов — по паспортам выбранных приборов, сверяются до разметки стен.
2. Высоты H — от чистого пола помещения, мм; отметка чистого пола и потолка — у левого края вида (от ±0,000 объекта). Привязки — от левого чистового угла вида (облицовка стен вычтена), как на развёртках стен.
3. Стояки в помещении: Ст K1-3 Ø110, Ст B1-3 Ø32, Ст T3-3 Ø32 — положение на плане выводов; выводы подключаются к ним по схеме разводки.
4. Ревизионные люки к арматуре и ревизиям в данных не заданы: место и размер не определены (записи реестра нет).
5. Часть подписей выводов не уместилась у знака: коды и высоты — в ведомости привязок.
6. Помещение «Санузел 2» — 2 листа: стены 1) А, Б; 2) В.
7. Расчёт систем водоснабжения и канализации и подбор оборудования выполняет проектная организация; лист задаёт места и высоты выводов.


	Лист	№ док.	Подпись	Дата
Дизайнер	Кырлан А.С.			04.11.26

Проект: Дом 331 м² — **М 1:20**

Развёртки мокрых зон: выводы ВК. Санузел 2 (лист 1 из 2)

Стадия	Лист	Листов
П	37	168

Стена В (М 1:20)

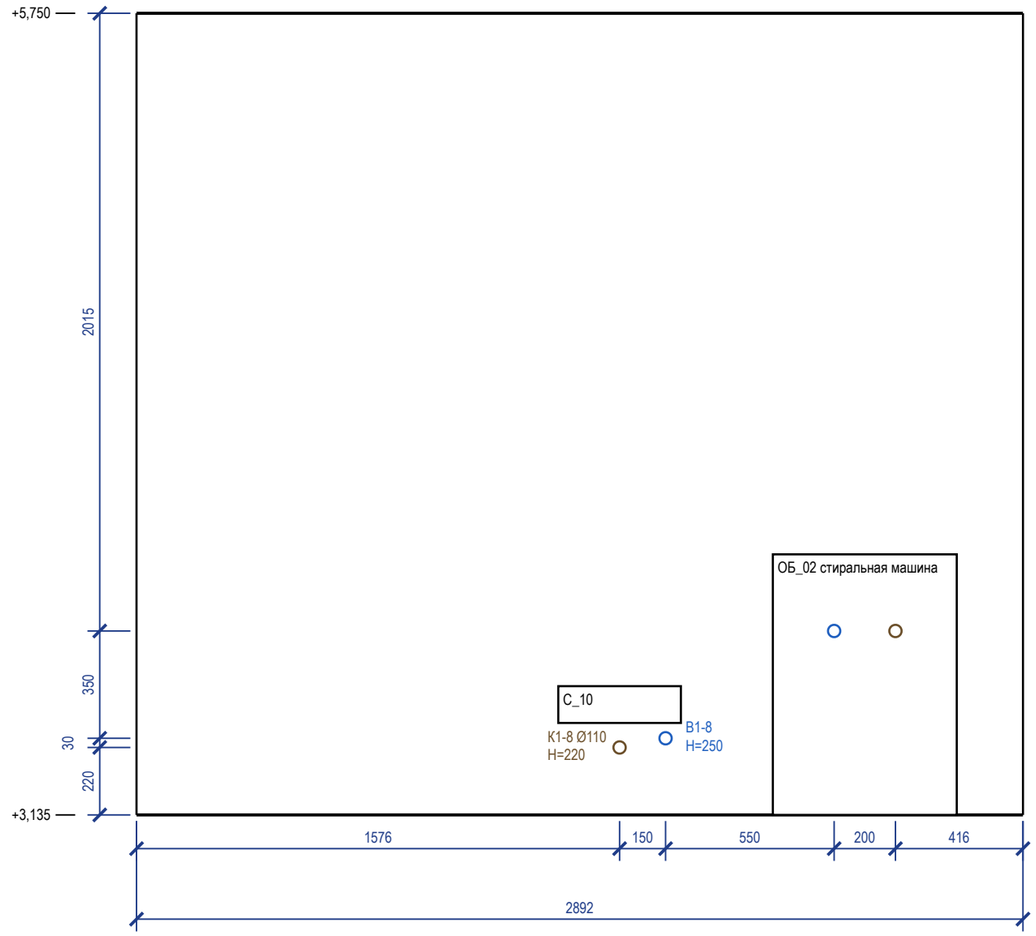

Ведомость привязок выводов (от чистого пола и угла)

Код	Прибор	Ø	H, мм	Привязка, мм
B1-8	C_10 унитаз подвесной	½"	250	ст. В: 1726 от лев. угла
K1-8	C_10 унитаз подвесной	Ø110	220	ст. В: 1576 от лев. угла
B1-10	ОБ_02 стиральная машина	½"	600	ст. В: 2276 от лев. угла
K1-10	ОБ_02 стиральная машина	Ø50	600	ст. В: 2476 от лев. угла

Условные обозначения

- вывод В1 (код — в ведомости привязок)
- вывод Т3 (код — в ведомости привязок)
- вывод К1 (код — в ведомости привязок)
- сантехприбор по расстановке (габарит модели)
- дверной проём; окно — сплошной контур

Примечания

1. Габариты и высоты приборов, межосевые смесителей и места кранов — по паспортам выбранных приборов, сверяются до разметки стен.
2. Высоты Н — от чистого пола помещения, мм; отметка чистого пола и потолка — у левого края вида (от ±0,000 объекта). Привязки — от левого чистового угла вида (облицовка стен вычтена), как на развёртках стен.
3. Стояки в помещении: Ст К1-3 Ø110, Ст В1-3 Ø32, Ст Т3-3 Ø32 — положение на плане выводов; выводы подключаются к ним по схеме разводки.
4. Ревизионные люки к арматуре и ревизиям в данных не заданы: место и размер не определены (записи реестра нет).
5. Часть подписей выводов не уместилась у знака: коды и высоты — в ведомости привязок.
6. Помещение «Санузел 2» — 2 листа: стены 1) А, Б; 2) В.
7. Расчёт систем водоснабжения и канализации и подбор оборудования выполняет проектная организация; лист задаёт места и высоты выводов.


					Проект: Дом 331 м²	М 1:20
	Лист	№ док.	Подпись	Дата		
Дизайнер	Кырлан А.С.			04.11.26	Развёртки мокрых зон: выводы ВК. Санузел 2 (лист 2 из 2)	Стадия: П; Лист: 38; Листов: 168

Поз.	Наименование и техническая характеристика	Тип, марка, обозначение документа	Код продукции	Поставщик	Ед. изм.	Кол.	Масса 1 ед., кг	Примечание
	Санитарные приборы							
1	Ванна встраиваемая акриловая 1700×750 мм, с каркасом, экраном и отверстием слив-перелив	аналог		выбор заказчика	шт	1		C_05
2	Унитаз подвесной безободковый, с сиденьем микролифт, крепёж и звукоизолирующая прокладка	Jacob Delafon Struktura EDF102-00		выбор заказчика	шт	3		C_02, C_06, C_10
3	Инсталляция для подвесного унитаза: рама высотой 1120 мм, бачок, клавиша смыва (ось клавиши 1050 мм от чистого пола)	аналог		выбор заказчика	шт	3		C_02, C_06, C_10; короб ГКЛВ
4	Раковина накладная 700×500 мм, на столешницу тумбы, с переливом	аналог		выбор заказчика	шт	1		C_03
5	Раковина накладная 1200×500 мм, на столешницу тумбы, с переливом	аналог		выбор заказчика	шт	1		C_07
6	Умывальник подвесной 600×450 мм, с отверстием под смеситель и переливом	аналог		выбор заказчика	шт	1		C_11
7	Поддон душевой низкий 900×1000 мм, с сифоном и выпуском Ø50, на ножках/подиуме	аналог		выбор заказчика	шт	1		C_09
8	Трап душевой с гидрозатвором и фланцем под гидроизоляцию, монтажная высота по паспорту	аналог		выбор заказчика	шт	1		C_01; узел 1 схема разводки
9	Мойка кухонная врезная / подстольная, с переливом, ориентир 700×480 мм — в модуле M_01 шириной 800 мм, вырез по шаблону модели	аналог		с кухонной мебелью	шт	1		M_01
10	Полотенцесушитель водяной (ГВС), с байпасом и кранами	аналог		выбор заказчика	шт	2		C_04, C_08
	Смесители, сифоны и арматура приборов							
11	Смеситель для ванны настенный однорычажный, межосевое 150 мм, с душевым набором (лейка, шланг, держатель)	аналог		выбор заказчика	шт	1		C_05
12	Смеситель для накладной раковины однорычажный, высокий излив, с донным клапаном	аналог		выбор заказчика	шт	2		C_03, C_07
13	Смеситель для умывальника однорычажный, с донным клапаном	аналог		выбор заказчика	шт	1		C_11
14	Душевая система скрытого монтажа с термостатом: встраиваемая часть, верхний душ, ручная лейка	аналог		выбор заказчика	шт	2		C_01, C_09; встраиваемая часть — до плитки
15	Смеситель кухонный однорычажный, высокий излив	аналог		выбор заказчика	шт	1		M_01
16	Обвязка ванны слив-перелив Ø40/50 с сифоном	аналог		выбор заказчика	шт	1		C_05
17	Сифон для умывальника бутылочный Ø32/40–50, с гофрой к выпуску	аналог		выбор заказчика	шт	3		C_03, C_07, C_11
18	Сифон для мойки Ø40/50	аналог		выбор заказчика	шт	1		M_01
19	Сифон для посудомоечной машины с обратным клапаном, на выводе слива Ø40	аналог		выбор заказчика	шт	1		M_02
20	Сифон для стиральной машины встраиваемый в стену Ø50, с обратным клапаном	аналог		выбор заказчика	шт	1		ОБ_02
21	Кран угловой ½"×½" с гибкой подводкой 40 см (умывальники, мойка)	аналог		выбор заказчика	шт	8		по 2 на прибор
22	Кран шаровой угловой ½"×¾" для подключения стиральной и посудомоечной машины	аналог		выбор заказчика	шт	2		ОБ_02, M_02
23	Узел подключения полотенцесушителя: байпас Ду20, краны шаровые ½" ×2	аналог		выбор заказчика	шт	2		
	Трубопроводы							
24	Труба полипропиленовая PP-R PN20 Ø20×3,4 (B1)	ГОСТ 32415-2013		выбор заказчика	м	32,5	0,17	21,5 + 7,6 + 10 %
25	Труба PP-R, армированная стекловолокном, PN20 Ø20×2,8 (Т3)	ГОСТ 32415-2013		выбор заказчика	м	39,5	0,15	25,2 + 10,3 + 10 %
26	Труба канализационная ПП Ø40 (К1)	ГОСТ 32414-2013		выбор заказчика	м	1		0,1 + 0,6 + 10 %
27	Труба канализационная ПП Ø50 (К1)	ГОСТ 32414-2013		выбор заказчика	м	17,5		13,1 + 2,7 + 10 %
28	Труба канализационная ПП Ø110 (К1)	ГОСТ 32414-2013		выбор заказчика	м	8,5		6,7 + 0,7 + 10 %
	Фасонные части и выводы							
29	Отвод канализационный ПП 45° Ø50	ГОСТ 32414-2013		выбор заказчика	шт	22		2 шт. на поворот
30	Отвод канализационный ПП 45° Ø110	ГОСТ 32414-2013		выбор заказчика	шт	16		2 шт. на поворот
31	Тройник канализационный ПП 45° (врезки ветвей)	ГОСТ 32414-2013		выбор заказчика	шт	11		
32	Ревизия канализационная ПП (после поворота трассы)	ГОСТ 32414-2013		выбор заказчика	шт	10		доступ сохранить
33	Фитинги PP-R Ø20: тройники, угольники 90° (ветви и повороты B1, Т3)	ГОСТ 32415-2013		выбор заказчика	шт	55		
34	Водорозетка PP-R Ø20×½" настенная, с креплением	ГОСТ 32415-2013		выбор заказчика	шт	23		коды — лист выводов
	Узлы ввода, люки, короба							
35	Кран шаровой латунный Ду15 PN16 (отключение ввода)	аналог		выбор заказчика	шт	6		Ст В1-1, Ст Т3-1, Ст В1-2, Ст Т3-2, Ст В1-3, Ст Т3-3
36	Фильтр сетчатый косой Ду15	аналог		выбор заказчика	шт	6		
37	Счётчик воды крыльчатый Ду15 (ХВ, ГВ), с поверкой	аналог		выбор заказчика	шт	6		пломба УК
38	Клапан обратный Ду15	аналог		выбор заказчика	шт	6		
39	Люк ревизионный нажимной под плитку 300×400 мм	аналог		выбор заказчика	шт	3		к стоякам и арматуре
40	Звукоизоляция стояка К1 в коробе: рулонный звукоизоляционный материал ≥ 10 мм, обмотка стояка на высоту этажа	аналог		выбор заказчика	м	8,4		Ст К1-1, Ст К1-2 (кухня), Ст К1-3
41	Короб К1 над полом: профиль ПН/ПС, ГКЛВ 12,5 мм под плитку	аналог		выбор заказчика	м	14,6		сечение — лист разводки

Примечания

1. Форма 1 ГОСТ 21.110-2013, ширины граф изменены по п. 4.1. «Аналог» — аналог по характеристикам: модели внести до черновых работ, привязки выводов сверить по паспортам.
2. Бытовая техника не входит (показана арматура подключения), мойка — в комплекте кухни (марка — модуля кухни, как у столяра). Длины труб — трасса листа разводки + подъёмы + 10 %.
3. Стояк К1 в коробе — звукоизоляция стояка в коробе без жёсткого контакта короба с трубой.
4. Расчёт систем водоснабжения и канализации, диаметры магистралей и подбор оборудования выполняет проектная организация.

					Проект: Дом 331 м²			
	Лист	№ док.	Подпись	Дата	Спецификация сантехнического оборудования	Стадия	Лист	Листов
Дизайнер	Кырлан А.С.			04.11.26		П	39	168

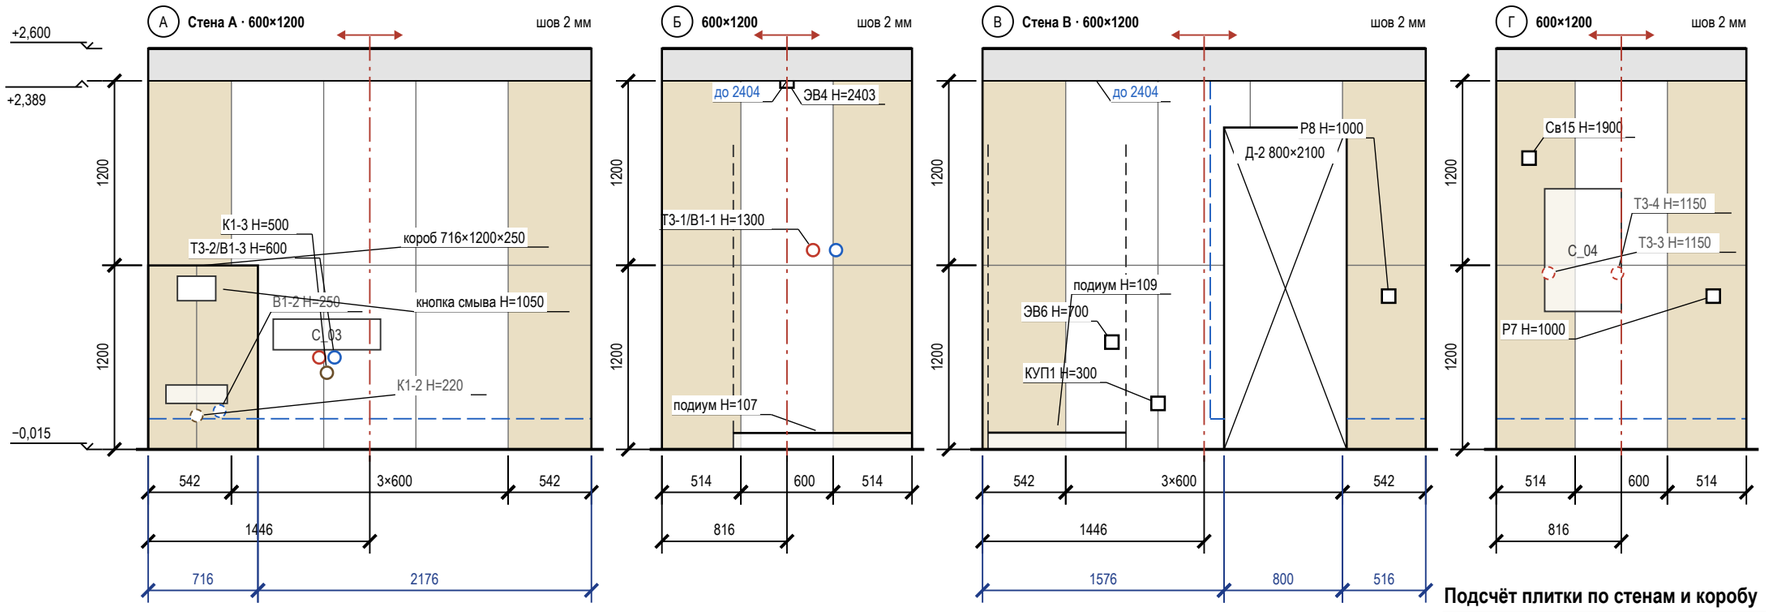

Условные обозначения

- плитка целая; тонкая линия — шов
- плитка с подрезкой (размер — на цепочке)
- ось старта; стрелки — направление укладки
- верх гидроизоляции: 200 от ЧП, в мокрой зоне — «до …»
- проём — не облицовывается
- сантехприбор: габарит, высота по практике
- граница душевой зоны (ограждение)
- короб инсталляции, в нём кнопка смыва 250×160
- вывод В1 (код — в ведомости привязок)
- вывод Т3 (код — в ведомости привязок)
- вывод К1 (код — в ведомости привязок)
- вывод за прибором / в коробе (не на сетке)
- электроточка: марка и Н — по листам ЭОМ
- отметка уровня, м: ±0,000 — чистый пол 1-го этажа
- низ потолка; серая полоса — стена без плитки
- А — обозначение стены А–Г (как на развёртках)


Примечания

1. Вид изнутри, стены по часовой стрелке А → Г. Высоты — от чистого пола (−0,015), отметки — от ±0,000 (чистый пол 1-го этажа). Раскладка от чистовых размеров (штукатурка 10 + клей 5 + плитка 9 мм), подрезки чистые; старт — от оси стены, ряды от пола целыми.
2. Облицовка не до потолка: верх плитки +2,389, выше — отделка стены по ведомости отделки до потолка +2,600; торец облицовки — профиль-окантовка.
3. Открытые выводы и электроточки — на шве или в центре плитки (допуск 10 мм; плитка от 900 мм по высоте на шве или не ближе 60 мм к нему).
4. Выводы ВК стоят по оси прибора и с прибором не двигаются — привязки по «Плану выводов сантехники» без сдвига; вне сетки (Т3-2/В1-3, К1-3, Т3-1/В1-1) — отверстие в плитке коронкой по той же привязке, плитку не сдвигать.
5. За приборами и в коробе (В1-2, К1-2, Т3-3, Т3-4) — штриховым кольцом.
6. Подиум душа С_01: верх у решётки трапа +0,085 (h 100 мм), к стенам поднимается уклоном к трапу — «подиум Н=…» на развёртке — верх подиума у этой стены; облицовка стен в зоне душа — от верха подиума, грань ступени — плиткой пола. Выводы В1-1, Т3-1: Н=1300 от чистого пола помещения = 1200 от верха подиума у трапа.
7. Гидроизоляция: 200 мм от ЧП по периметру; у душа — на всю высоту стен душевой зоны и 500 мм за край душевой зоны (СП 29.13330.2011, п. 7.2 — на высоту замачивания); углы — лентой; акт скрытых работ, пролив.
8. Короб 716×1200×250: лицо 315 / 399 мм от оси кнопки смыва, боковины, полка; углы — запил 45° или профиль; за коробом плитку не кладут.

Подсчёт плитки по стенам и коробу

Поверхность	L × H, мм	S, м²	Целых	Подр.	С запасом	Подрезки: край / верх, мм
стена А	2892 × 2404	6,21	5	4	10	542 / 542; целый ряд
короб (ст. А)	716×1200×250	1,64	0	6	7	лицо 315 / 399; бок. 250
стена Б	1632 × 2404	4,04	2	4	7	514 / 514; целый ряд
стена В	2892 × 2404	5,39	2	7	10	542 / 542; целый ряд
стена Г	1632 × 2404	4,04	2	4	7	514 / 514; целый ряд
Итого		**21,31**	**11**	**25**	**41**	

					Проект: Дом 331 м²	**М 1:40**
	Лист	№ док.	Подпись	Дата	Раскладка плитки. Санузел 1 этажа. Развёртки стен	Стадия / Лист / Листов
Дизайнер	Кырлан А.С.			04.11.26		П / 40 / 168

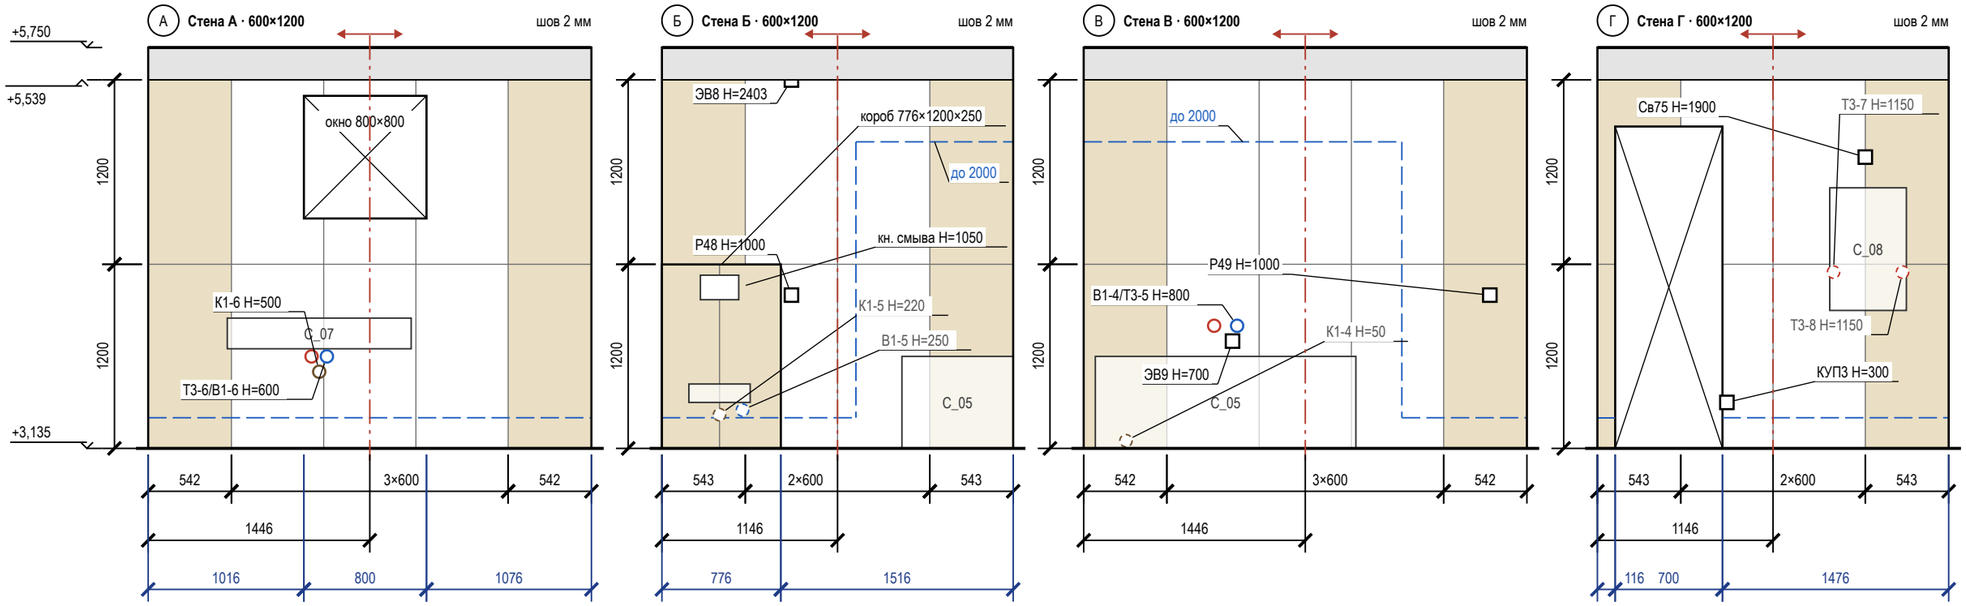

Подсчёт плитки по стенам и коробу

Поверхность	L × H, мм	S, м²	Целых	Подр.	С запасом	Подрезки: край / верх, мм
стена А	2892 × 2404	4,54	3	7	11	542 / 542; целый ряд
стена Б	2292 × 2404	3,97	3	4	8	543 / 543; целый ряд
короб (ст. Б)	776×1200×250	1,73	0	6	7	лицо 375 / 399; бок. 250
стена В	2892 × 2404	7,07	6	4	11	542 / 542; целый ряд
стена Г	2292 × 2404	3,43	2	6	9	543 / 543; целый ряд
Итого		**20,73**	**14**	**27**	**46**	

Сдвиг точек под раскладку

Точка (ВК, ЭОМ)	Стена	Проект: от угла / H	Под раскладку: от угла / H	Сдвиг, мм
ЭВ9	В	971 / 700	844 / 700	−127 в центр плитки

Условные обозначения


- плитка целая; тонкая линия — шов
- плитка с подрезкой (размер — на цепочке)
- ось старта; стрелки — направление укладки
- верх гидроизоляции: 200 от ЧП, в мокрой зоне — «до …»
- проём — не облицовывается
- сантехприбор: габарит, высота по практике
- короб инсталляции, в нём кнопка смыва 250×160
- вывод В1 (код — в ведомости привязок)
- вывод Т3 (код — в ведомости привязок)
- вывод К1 (код — в ведомости привязок)
- вывод за прибором / в коробе (не на сетке)
- электроточка: марка и H — по листам ЭОМ
- отметка уровня, м: ±0,000 — чистый пол 1-го этажа
- низ потолка; серая полоса — стена без плитки
- А — обозначение стены А–Г (как на развёртках)

Примечания

1. Вид изнутри, стены по часовой стрелке А → Г. Высоты — от чистого пола (+3,135), отметки — от ±0,000 (чистый пол 1-го этажа). Раскладка от чистовых размеров (штукатурка 10 + клей 5 + плитка 9 мм), подрезки чистые; старт — от оси стены, ряды от пола целыми.
2. Облицовка не до потолка: верх плитки +5,539, выше — отделка стены по ведомости отделки до потолка +5,750; торец облицовки — профиль-окантовка.
3. Точки из таблицы сдвигов переносятся до черновой разводки (ЭОМ — по тем же числам).
4. Выводы ВК стоят по оси прибора и с прибором не двигаются — привязки по «Плану выводов сантехники» без сдвига; вне сетки (Т3-6/В1-6, К1-6, В1-4/Т3-5) отверстие в плитке коронкой по той же привязке, плитку не сдвигать.
5. За приборами и в коробе (В1-5, К1-5, К1-4, Т3-7, Т3-8) — штриховым кольцом.
6. Гидроизоляция: 200 мм от ЧП по периметру; над ванной — до 2000 и 300 мм за борт (СП 29.13330.2011, п. 7.2 — на высоту замачивания); углы — лентой; акт скрытых работ, пролив.
7. Короб 776×1200×250: лицо 375 / 399 мм от оси кнопки смыва, боковины, полка; углы — запил 45° или профиль; за коробом плитку не кладут.

					Проект: Дом 331 м² — **М 1:40**
	Лист	№ док.	Подпись	Дата	Раскладка плитки. Санузел мастер. Развёртки стен
Дизайнер	Кырлан А.С.			04.11.26	

Стадия	Лист	Листов
П	41	168

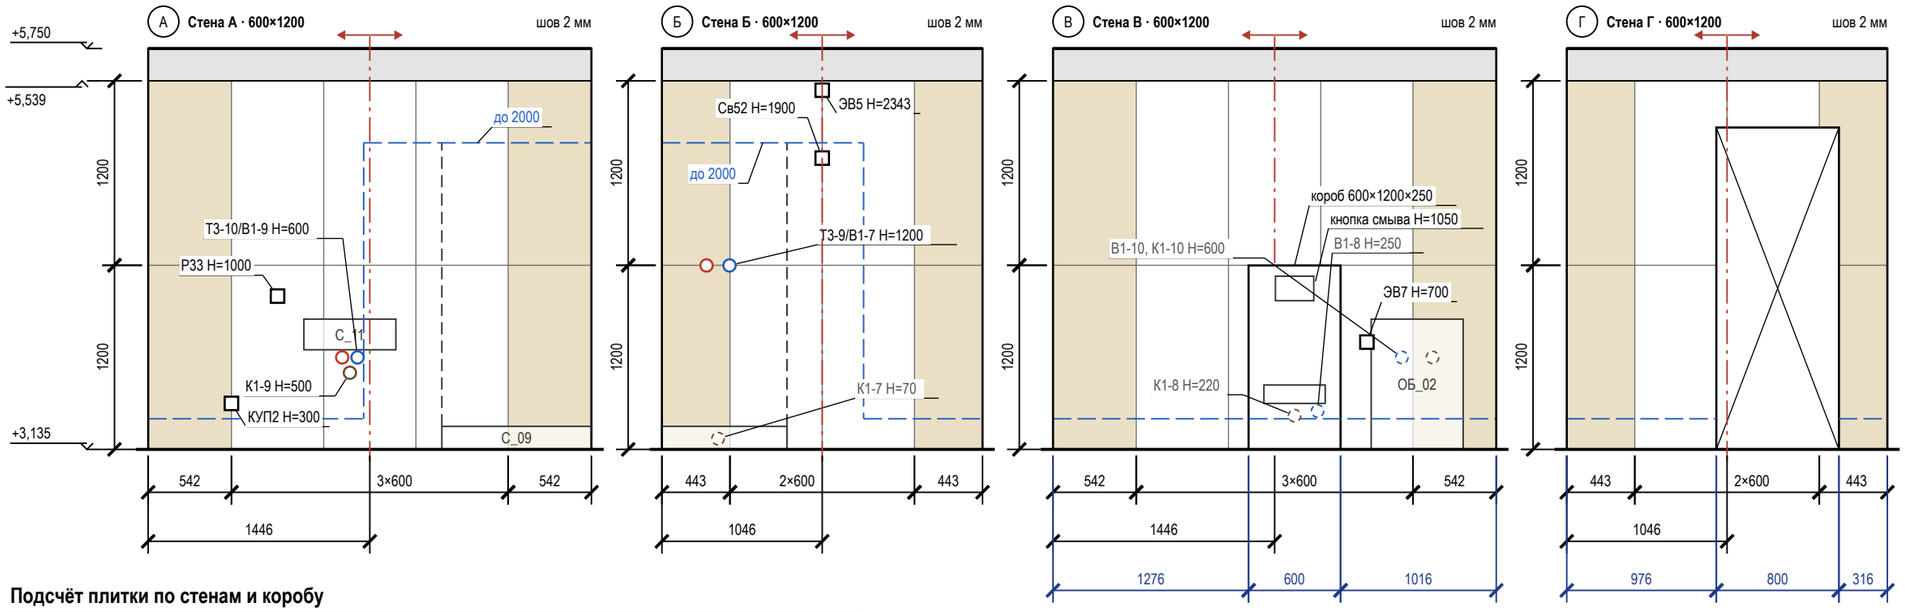

Подсчёт плитки по стенам и коробу

Поверхность	L × H, мм	S, м²	Целых	Подр.	С запасом	Подрезки: край / верх, мм
стена А	2892 × 2404	7,07	6	4	11	542 / 542; целый ряд
стена Б	2092 × 2404	4,42	4	4	9	443 / 443; целый ряд
стена В	2892 × 2404	2,81	4	6	11	542 / 542; целый ряд
короб (ст. В)	600×1200×250	1,47	1	3	5	лицо 600; бок. 250
стена Г	2092 × 2404	2,74	0	7	8	443 / 443; целый ряд
Итого		**18,51**	**15**	**24**	**44**	

Условные обозначения


- плитка целая; тонкая линия — шов
- плитка с подрезкой (размер — на цепочке)
- ось старта; стрелки — направление укладки
- верх гидроизоляции: 200 от ЧП, в мокрой зоне — «до …»
- проём — не облицовывается
- сантехприбор: габарит, высота по практике
- граница душевой зоны (ограждение)
- короб инсталляции, в нём кнопка смыва 250×160
- вывод В1 (код — в ведомости привязок)
- вывод Т3 (код — в ведомости привязок)
- вывод К1 (код — в ведомости привязок)
- вывод за прибором / в коробе (не на сетке)
- электроточка: марка и H — по листам ЭОМ
- отметка уровня, м: ±0,000 — чистый пол 1-го этажа
- низ потолка; серая полоса — стена без плитки
- (А) обозначение стены А–Г (как на развёртках)

Примечания

1. Вид изнутри, стены по часовой стрелке А → Г. Высоты — от чистого пола (+3,135), отметки — от ±0,000 (чистый пол 1-го этажа). Раскладка от чистовых размеров (штукатурка 10 + клей 5 + плитка 9 мм), подрезки чистые; старт — от оси стены, ряды от пола целыми.
2. Облицовка не до потолка: верх плитки +5,539, выше — отделка стены по ведомости отделки до потолка +5,750; торец облицовки — профиль-окантовка.
3. Открытые выводы и электроточки — на шве или в центре плитки (допуск 10 мм; плитка от 900 мм по высоте на шве или не ближе 60 мм к нему).
4. Выводы ВК стоят по оси прибора и с прибором не двигаются — привязки по «Плану выводов сантехники» без сдвига; вне сетки (Т3-10/В1-9, К1-9, Т3-9/В1-7) — отверстие в плитке коронкой по той же привязке, плитку не сдвигать.
5. За приборами и в коробе (К1-7, В1-8, К1-8, В1-10, К1-10) — штриховым кольцом.
6. Гидроизоляция: 200 мм от ЧП по периметру; у душа — до 2000 и 500 мм за поддон (СП 29.13330.2011, п. 7.2 — на высоту замачивания); углы — лентой; акт скрытых работ, пролив.
7. Короб 600×1200×250: лицо 600 мм от оси кнопки смыва, боковины, полка; углы — запил 45° или профиль; за коробом плитку не кладут.

					Проект: Дом 331 м² — **М 1:40**
	Лист	№ док.	Подпись	Дата	Раскладка плитки. Санузел 2. Развёртки стен
Дизайнер	Кырлан А.С.			04.11.26	

Стадия	Лист	Листов
П	42	168

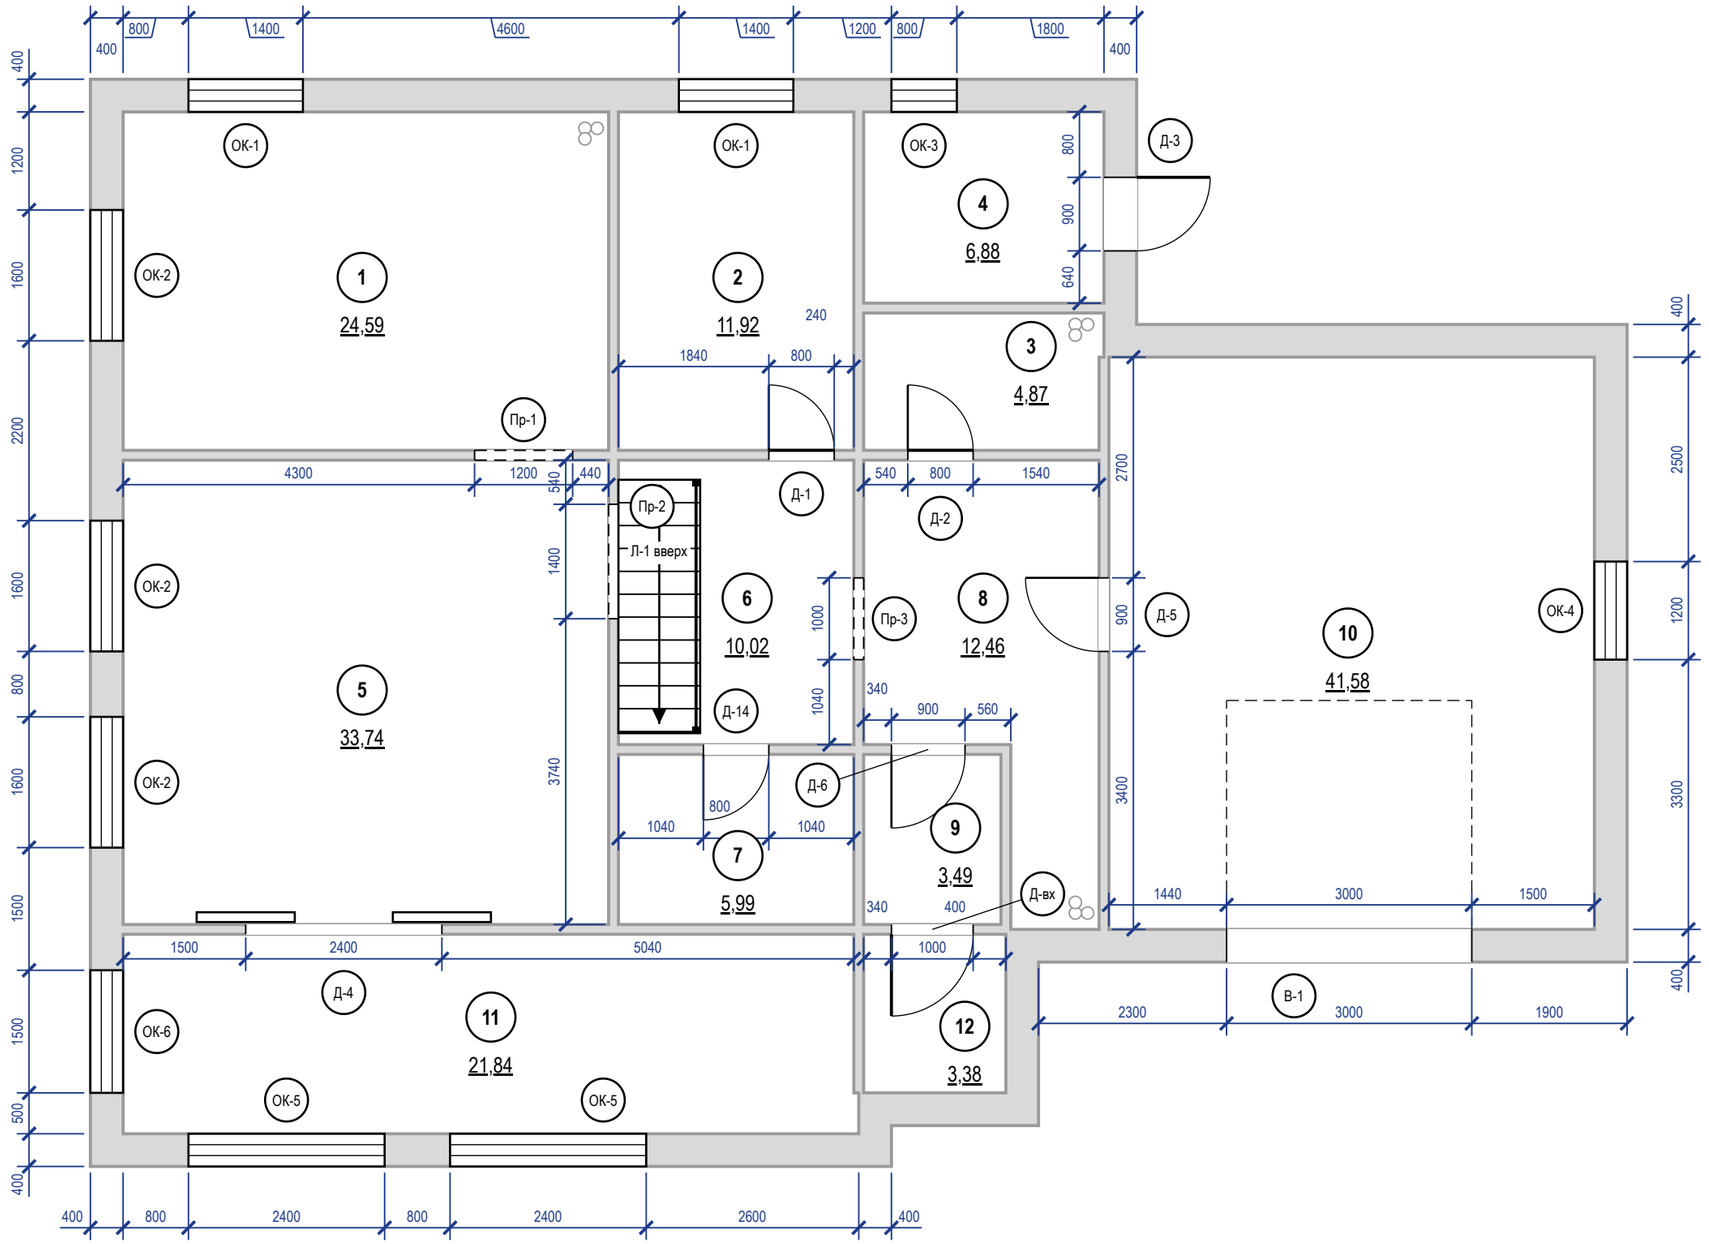


Примечания

1. Размеры проёмов и привязки — в миллиметрах от чистых граней стен до отделки; привязка — от угла того помещения, со стороны которого стоит размер. Размер проёма — ширина × высота от чистого пола 0,000. Размеры на плане — проёмов, не полотен: полотно — в ведомости, коробка — по системе.
2. Марки в кружках — типы заполнения проёмов (ГОСТ 21.501-2018, п. 5.3.2); одна марка — один типоразмер; количество сверено с планом.
3. Д-1, Д-2 — существующие проёмы, до техзаключения не расширять.
4. Ведомость заполнения проёмов, открывание полотен, заказ и порядок монтажа блоков — лист 45.

					Проект: Дом 331 м²	М 1:75
	Лист	№ док.	Подпись	Дата		
Дизайнер	Кырлан А.С.			04.11.26	План размещения дверей · 1-й этаж	Стадия: П; Лист: 43; Листов: 168

выпуск 04.11.2026 № f163a372b2 · стр. 43 из 168

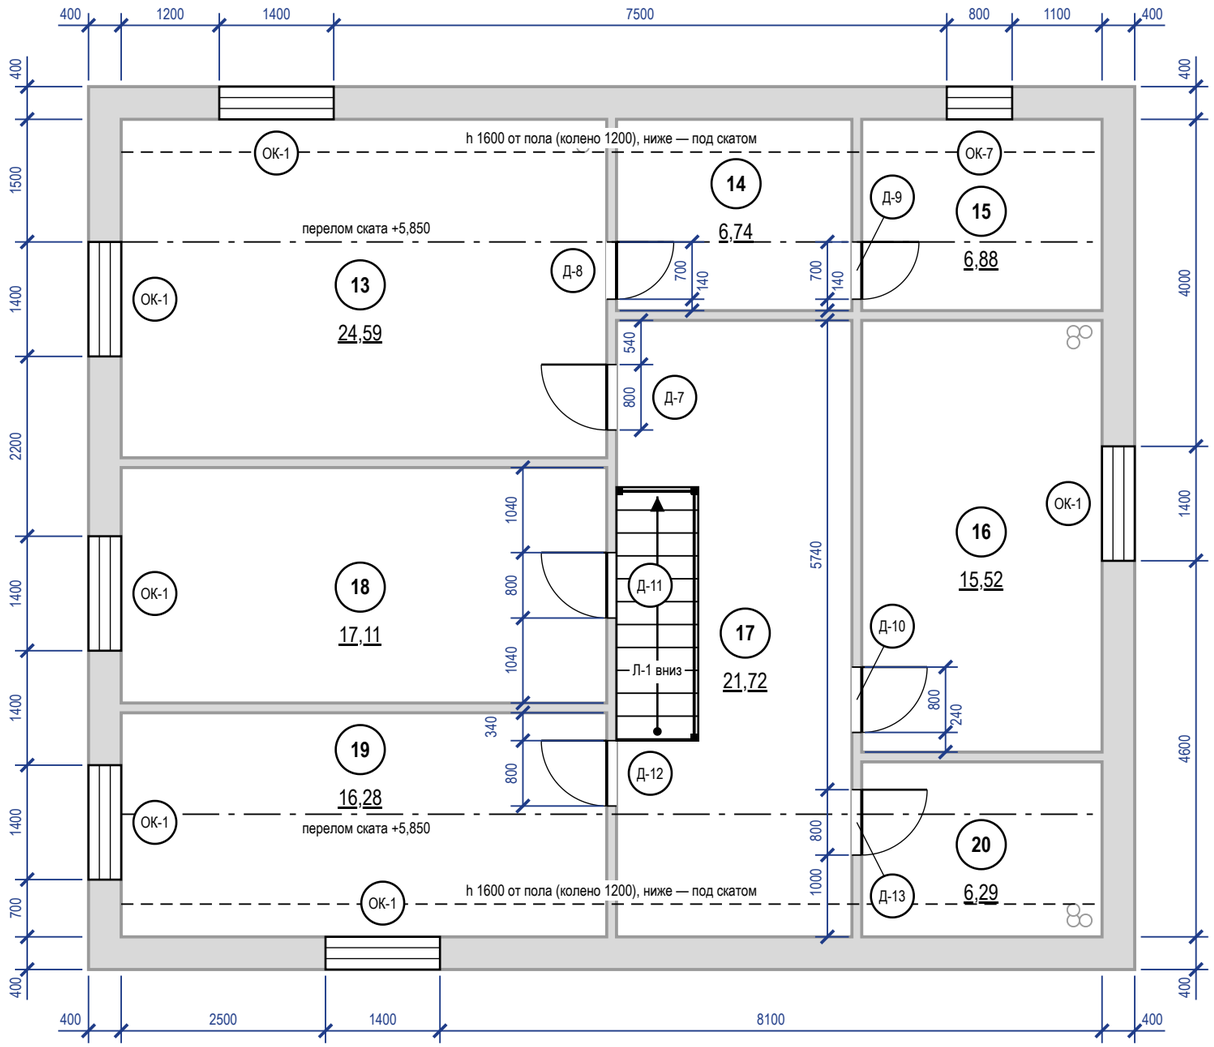

Примечания

1. Размеры проёмов и привязки — в миллиметрах от чистых граней стен до отделки; привязка — от угла того помещения, со стороны которого стоит размер. Размер проёма — ширина × высота от чистого пола 0,000. Размеры на плане — проёмов, не полотен: полотно — в ведомости, коробка — по системе. Откос от угла помещения до проёма с коробкой — не менее 50 мм.
2. Марки в кружках — типы заполнения проёмов (ГОСТ 21.501-2018, п. 5.3.2); одна марка — один типоразмер; количество сверено с планом.
3. Д-7…Д-13 — существующие проёмы, до техзаключения не расширять.
4. Ведомость заполнения проёмов, открывание полотен, заказ и порядок монтажа блоков — лист 45.

					Проект: Дом 331 м²	М 1:75
	Лист	№ док.	Подпись	Дата		
Дизайнер	Кырлан А.С.			04.11.26	План размещения дверей · Мансарда	Стадия: П; Лист: 44; Листов: 168

выпуск 04.11.2026 № f163a372b2 · стр. 44 из 168


Ведомость заполнения проёмов

Марка	Наименование, обозначение	Проём ш×в, мм	Полотно (расч.)	Кол.	Откр.	Отделка полотна	Фурнитура	Прим.
Д-вх	Блок дверной входной, ГОСТ 31173-2016	1000×2100	блок задать	1	Л	в комплекте блока	в комплекте блока (замки, глазок)	наружу
В-1	Ворота подъёмно-секционные, по каталогу изготовителя	3000×2300	не задано (записи реестра нет)	1		в комплекте ворот	в комплекте ворот (направляющие, привод)	
Д-1	Дверь скрытого монтажа, UNION FILO-60 Piatto	800×2100	700×2000	1	П	окраска No. 226 с двух сторон	скрытые петли 3D, магнитный замок	
Д-2	Дверь скрытого монтажа, UNION FILO-60 Piatto	800×2100	700×2000	1	П	в тон облицовки — пом. 3, No. 226 — пом. 8	скрытые петли 3D, магнитный замок, фиксатор WC	порог 15
Д-3	Блок дверной входной, ГОСТ 31173-2016	900×2100	блок задать	1	П	в комплекте блока	в комплекте блока (замки, глазок)	наружу
Д-4	Дверь раздвижная двустворчатая, остекл., ГОСТ 475-2016	2400×2100	не задано (записи реестра нет)	1			раздвижная система, ручки-купе	
Д-5	Блок дверной внутренний, ГОСТ 475-2016	900×2100	800×2000	1	Л		петли, ручка с защёлкой	пом. 8; EI 30
Д-6	Блок дверной внутренний, ГОСТ 475-2016	900×2100	800×2000	1	Л		петли, ручка с защёлкой	
Д-7	Дверь скрытого монтажа, UNION FILO-60 Piatto	800×2100	700×2000	1	Л	окраска No. 226 с двух сторон	скрытые петли 3D, магнитный замок	
Д-8	Дверь скрытого монтажа, UNION FILO-60 Piatto	700×2100	600×2000	1	П	No. 105 — пом. 14, No. 226 — пом. 13	скрытые петли 3D, магнитный замок	
Д-9	Дверь скрытого монтажа, UNION FILO-60 Piatto	700×2100	600×2000	1	П	в тон облицовки — пом. 15, No. 105 — пом. 14	скрытые петли 3D, магнитный замок, фиксатор WC	порог 15
Д-10	Дверь скрытого монтажа, UNION FILO-60 Piatto	800×2100	700×2000	1	П	окраска No. 226 с двух сторон	скрытые петли 3D, магнитный замок	
Д-11	Дверь скрытого монтажа, UNION FILO-60 Piatto	800×2100	700×2000	1	Л	окраска No. 226 с двух сторон	скрытые петли 3D, магнитный замок	
Д-12	Дверь скрытого монтажа, UNION FILO-60 Piatto	800×2100	700×2000	1	Л	окраска No. 226 с двух сторон	скрытые петли 3D, магнитный замок	
Д-13	Дверь скрытого монтажа, UNION FILO-60 Piatto	800×2100	700×2000	1	П	в тон облицовки — пом. 20, No. 226 — пом. 17	скрытые петли 3D, магнитный замок, фиксатор WC	порог 15
Д-14	Блок дверной внутренний, ГОСТ 475-2016	800×2100	700×2000	1	Л		петли, ручка с защёлкой	
Пр-1	Портал без заполнения	1200×2100		1				б/п
Пр-2	Портал без заполнения	1400×2100		1				б/п
Пр-3	Портал без заполнения	1000×2100		1				б/п
ОК-1	Блок оконный, ГОСТ 23166-2021	1400×1500		8				низ 900
ОК-2	Блок оконный, ГОСТ 23166-2021	1600×1500		3				низ 900
ОК-3	Блок оконный, ГОСТ 23166-2021	800×900		1				низ 1200
ОК-4	Блок оконный, ГОСТ 23166-2021	1200×900		1				низ 1200
ОК-5	Блок оконный, ГОСТ 23166-2021	2400×1600		2				низ 900
ОК-6	Блок оконный, ГОСТ 23166-2021	1500×1600		1				низ 900
ОК-7	Блок оконный, ГОСТ 23166-2021	800×800		1				низ 1500

Примечания


1. Марки проёмов — те же, что на планах дверей этажей (листы 43, 44); привязки проёмов — там же; количество — по всем этажам дома.
2. Открывание: Л — петли слева, П — справа, если смотреть со стороны, куда открывается полотно (на себя).
3. Дверные блоки обычного монтажа (Д-4…Д-6, Д-14) заказывать после чистовой стяжки и штукатурки, проёмы перемерить; монтажный зазор коробки 10–15 мм на сторону, откос от угла помещения до коробки — не менее 50 мм.
4. Скрытые двери (Д-1, Д-2, Д-7…Д-13): проём замерить в чистоте; блок заказать до штукатурки (≈ 30 дн.), короб ставить до штукатурки; полотно навесить после чистовой отделки, красить в цвет стен. Порядок — практика монтажа, изготовитель подтверждает.
5. Полотно «расч.» — по проёму и ряду изделия с запасом по каталогам, заказ — по таблице проёмов модели; Д-1, Д-2, Д-7…Д-13: проём 2100, а под полотно 2000 по каталогам нужен 2050–2080, под 2100 — 2150–2180: высоту проёма — по модели; Д-5, Д-6, Д-14: проём 2100, а под полотно 2000 по каталогам нужен 2040–2080, под 2100 — 2140–2180: высоту проёма — по модели; Д-вх: входной блок по ГОСТ 31173-2016 — задать при выборе блока; Д-3: входной блок по ГОСТ 31173-2016 — задать при выборе блока; Д-4: раздвижная, полотно — по системе — полотно задать при выборе модели.

Схемы дверных блоков (1:40) — вид со стороны открывания; вершина треугольника — сторона петель — продолжение на листе 46

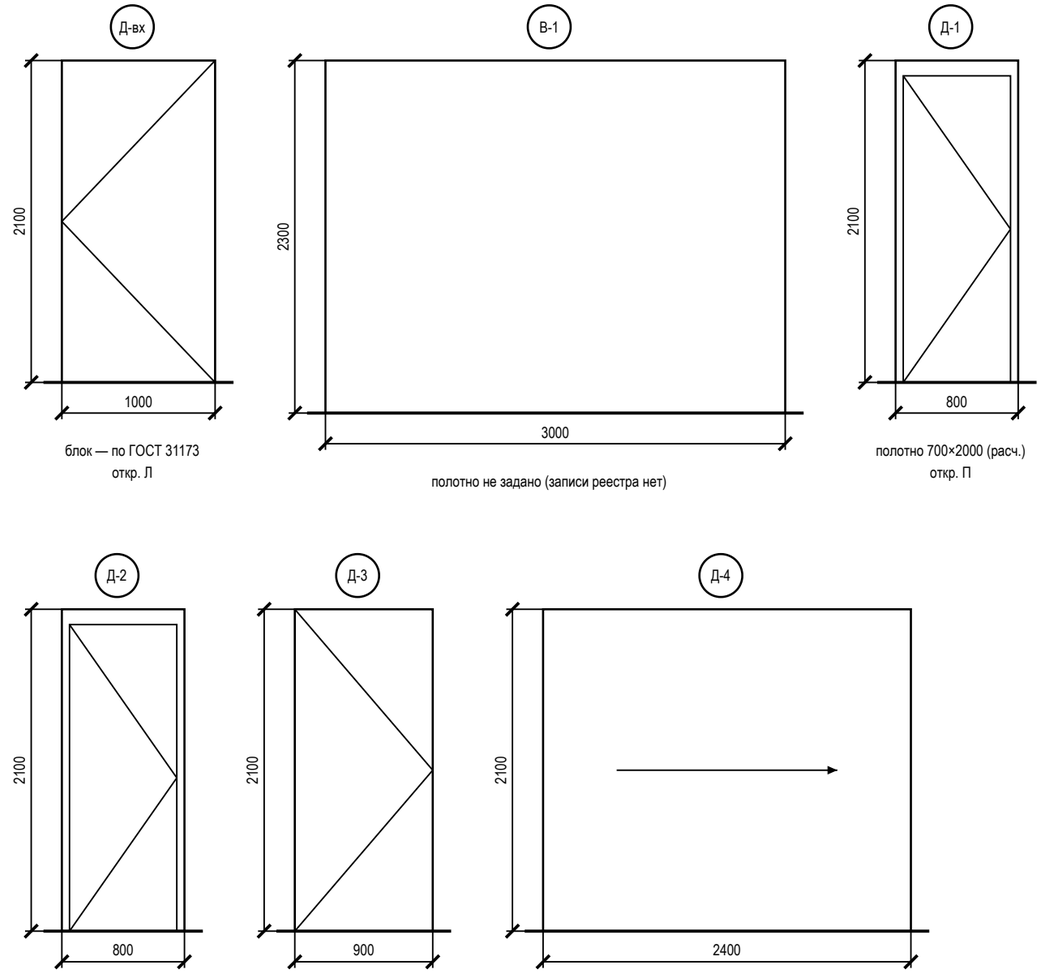


					Проект: Дом 331 м²	
	Лист	№ док.	Подпись	Дата		
Дизайнер	Кырлан А.С.			04.11.26	Ведомость заполнения проёмов	Стадия: П; Лист: 45; Листов: 168


Схемы дверных блоков (1:40) — вид со стороны открывания; вершина треугольника — сторона петель — продолжение; ведомость и примечания — лист 45

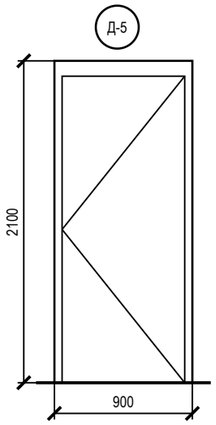


полотно 800×2000 (расч.)
откр. Л

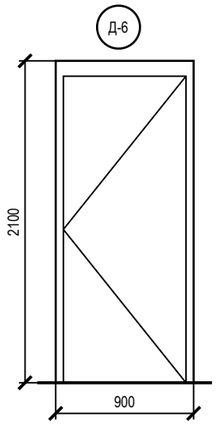


полотно 800×2000 (расч.)
откр. Л

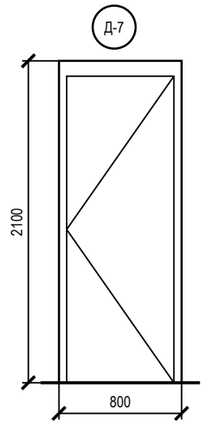


полотно 700×2000 (расч.)
откр. Л

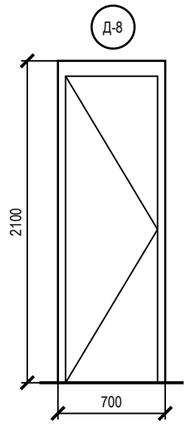


полотно 600×2000 (расч.)
откр. П

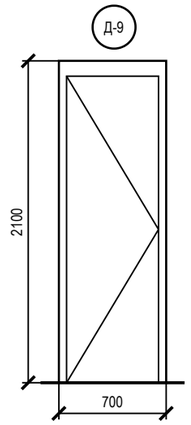


полотно 600×2000 (расч.)
откр. П

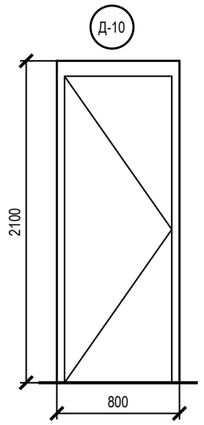


полотно 700×2000 (расч.)
откр. П

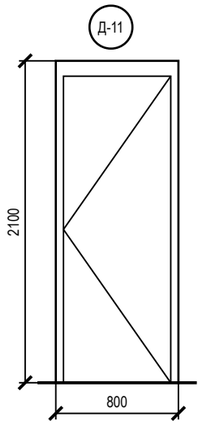


полотно 700×2000 (расч.)
откр. Л

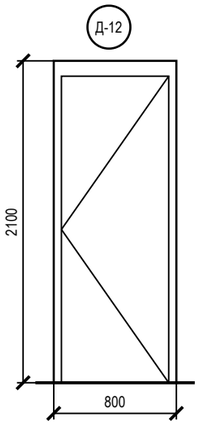


полотно 700×2000 (расч.)
откр. Л

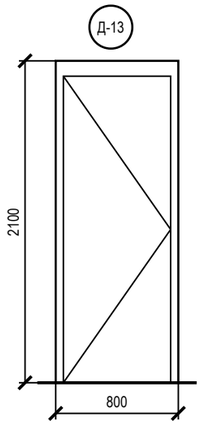


полотно 700×2000 (расч.)
откр. П

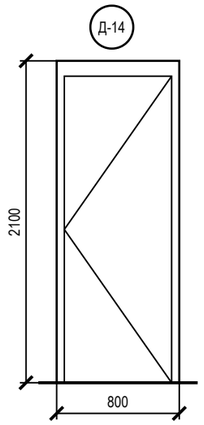


полотно 700×2000 (расч.)
откр. Л

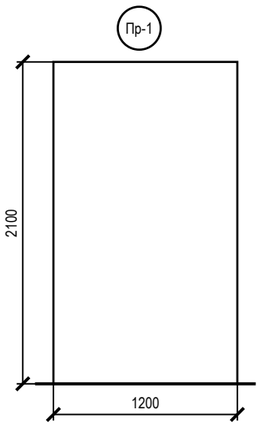

без заполнения

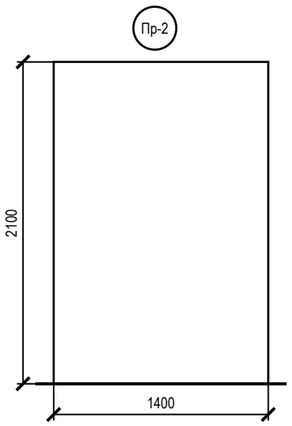

без заполнения

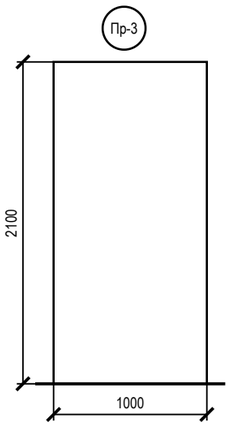


без заполнения


					Проект: Дом 331 м²
	Лист	№ док.	Подпись	Дата	Схемы дверных блоков
Дизайнер	Кырлан А.С.			04.11.26	

Стадия	Лист	Листов
П	46	168

План марша Л-1 (М 1:50) · 6. Холл с лестницей

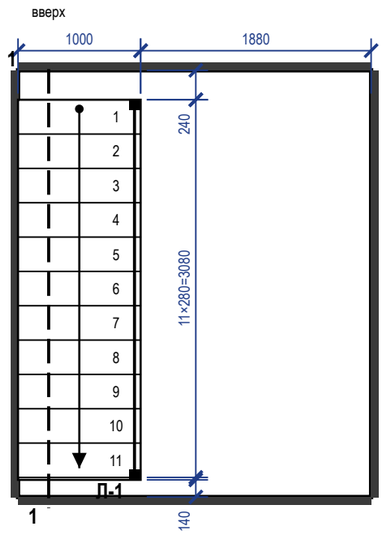


Разрез 1-1 (М 1:50)

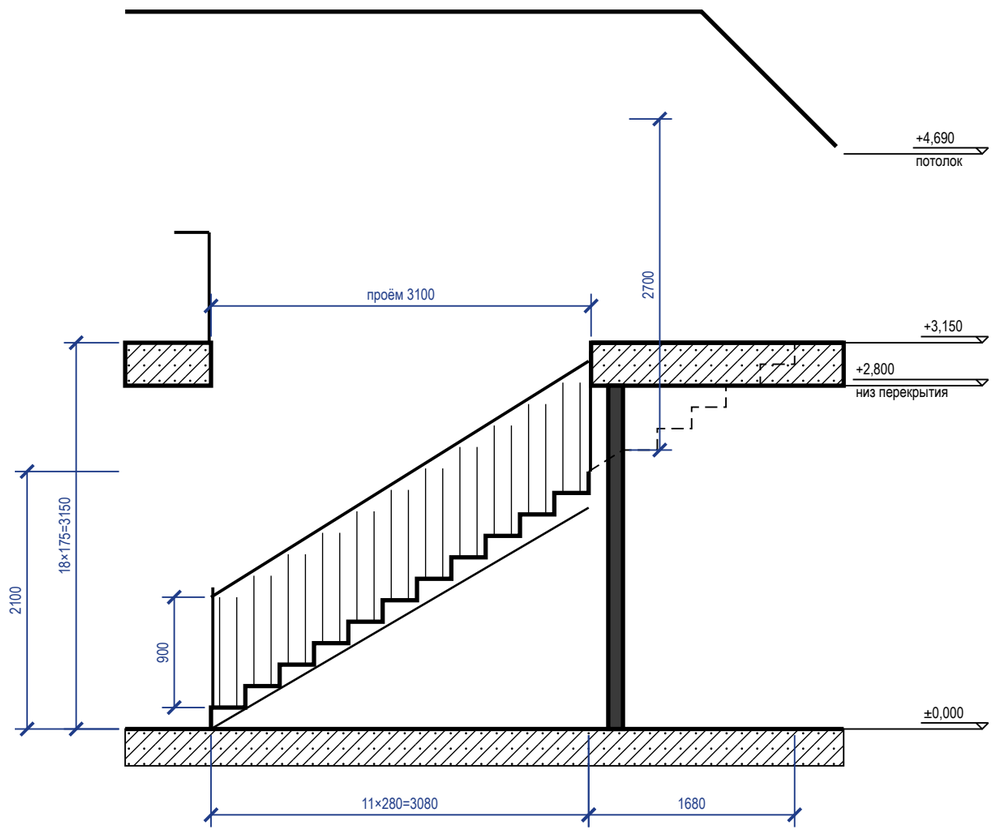

Спецификация элементов лестницы Л-1 — не для заказа

Поз.	Наименование	Кол.	Материал, сечение	Примечание
1	Ступень (проступь)	17	дуб, массив 40 мм, масло	1000×280; на черт. 11
2	Подступенок	18	дуб 18 мм	высота 175; на черт. 12
3	Косоур	2	косоуры стальные 80×40×4, порошковая окраска	несущие марша
4	Столб ограждения марша	2	сталь 20×20, порошковая окраска	по концам марша, стороны Б
5	Балясина	46	сталь 20×20, порошковая окраска	шаг 120, просвет 100
6	Поручень марша	1	дуб 40×60	L ≈ 5,61 м, h 900
7	Столб ограждения проёма	3	сталь 20×20, порошковая окраска	углы проёма, стороны А, Б
8	Балясина ограждения проёма	34	сталь 20×20, порошковая окраска	шаг 120
9	Поручень ограждения проёма	1	дуб 40×60	L ≈ 4,10 м, h 900
10	Крепёж ограждения	1	комплект по изделию	нагрузка на поручень 0,5 кН/м

Узел 1. Крепление стойки ограждения (М 1:5)

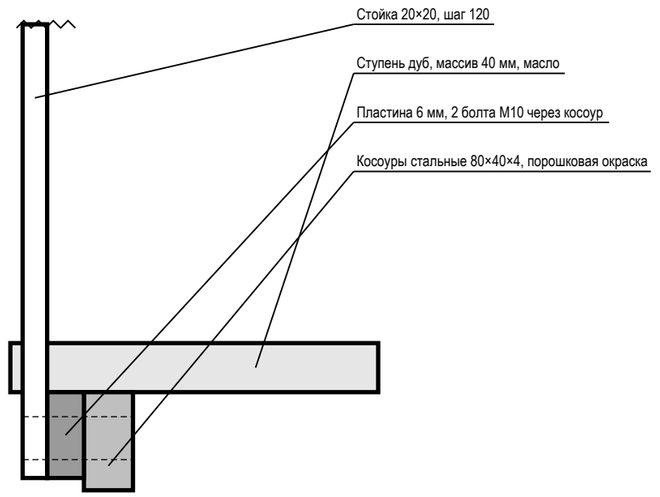


Зазор от низа заполнения до ступени — не более 100 (ГОСТ 25772-2025, прил. А, прим. 3)

Примечания

1. Лестница Л-1: 18 подъёмов × 175 мм = 3150 мм (отм. ±0,000 … +3,150), проступь 280 мм, ширина марша 1000 мм; уклон 32,0°, шаг 2h + b = 630 мм (удобно 600–640 — практика).
2. В габарит марша 3100 мм входят 11 проступей (до отм. +2,100); до пола этажа выше нужно 17 проступей — 4760 мм (показаны штрихом): одномаршевая лестница в этом помещении не встаёт, решение по реестру. Спецификация — расчёт на марш до пола этажа выше, не для заказа: количества пересчитать после решения по типу лестницы.
3. Ограждение марша со стороны Б: балясины, просвет между элементами 100 мм (не больше 150 — ГОСТ 25772-2025, табл. 3, тип МВ); высота 900 мм, поручень с одной стороны на 900 мм по линии носков (не менее 900 — СП 55.13330.2016, п. 8.3; СП 59.13330.2020, п. 6.2.11).
4. Проём в перекрытии 1000×3100 мм на этаже 2 ограждён со сторон А, Б высотой 900 мм, непрерывно, с поручнем (СП 55.13330.2016, п. 8.3); нагрузка на поручень 0,5 кН/м (СП 20.13330.2016, п. 8.2.6).
5. Просвет над линией носков — не менее 2700 мм (ступень 13, под потолком мансарды); рекомендуется не менее 2000, путь эвакуации — 2200 (СП 55.13330.2016, п. 7.4).
6. Все подступенки одной высоты (СП 55.13330.2016, п. 8.2). Разность отметок чистых полов замерить до заказа изделия: высота подступенка — по замеру.
7. Узел 1 — типовое решение крепления стойки к косоуру; крепёж, сечения и материал — по проекту изделия изготовителя лестницы.

					Проект: Дом 331 м²	М 1:50
	Лист	№ док.	Подпись	Дата		
Дизайнер	Кырлан А.С.			04.11.26	Лестница Л-1	Стадия / Лист / Листов
						П / 47 / 168

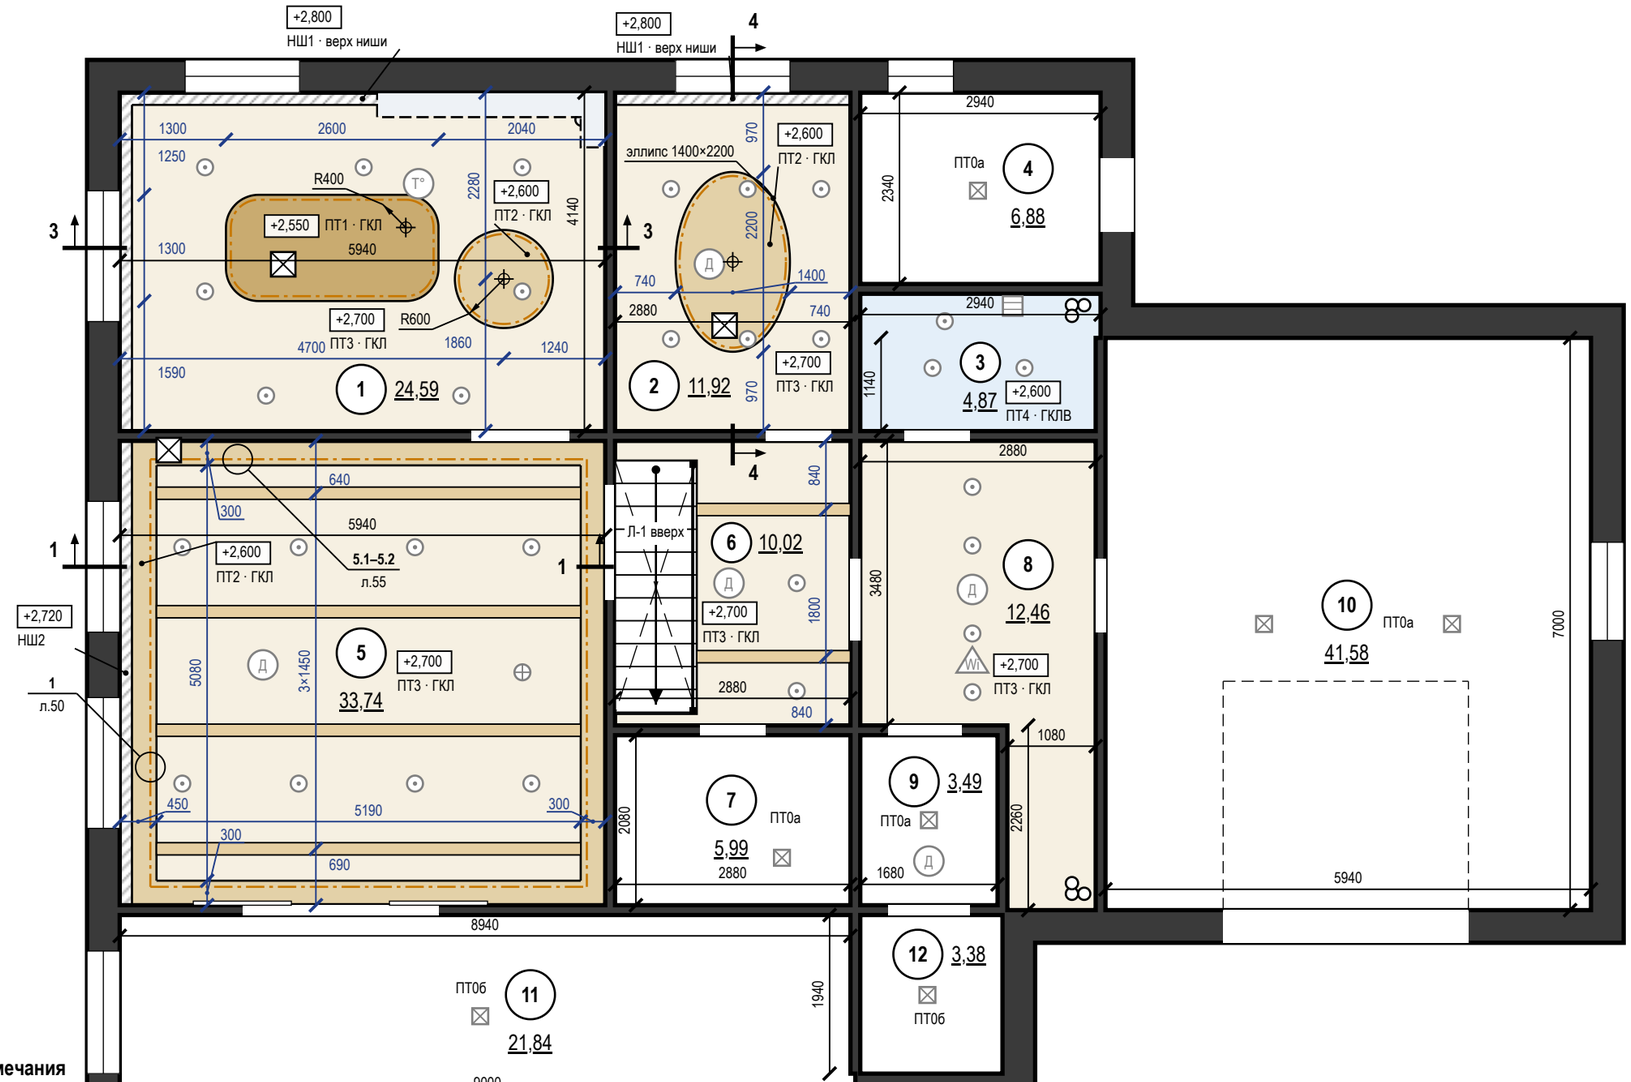

Ведомость потолков

Пом.	Марка	Конструкция	Низ / верх ниши	S, м²	Q
1	ПТ1	ГКЛ П113, остров + LED	+2,550	3,24	Q3
1	ПТ2	ГКЛ П113, круг + LED	+2,600	1,13	Q3
1	ПТ3	ГКЛ П113	+2,700	18,73	Q3
1	НШ1	ниша под шторы 150×100	+2,800	1,49	
2	ПТ2	ГКЛ П113, эллипс + LED	+2,600	2,42	Q3
2	ПТ3	ГКЛ П113	+2,700	9,07	Q3
2	НШ1	ниша под шторы 150×100	+2,800	0,43	
3	ПТ4	ГКЛВ П113	+2,600	4,87	Q3
4, 7, 9, 10	ПТ0а	Потолок под покраску	+2,800	57,94	
5	ПТ2	ГКЛ П113, короб LED	+2,600	6,52	Q3
5	ПТ3	ГКЛ П113	+2,700	26,37	Q3
5	НШ2	ниша под шторы 150×120	+2,720	0,85	
6	ПТ3	ГКЛ П113	+2,700	6,92	Q3
8	ПТ3	То же	+2,700	12,46	Q3
11, 12	ПТ0б	Потолок под покраску (летнее помещение)	+2,800	25,22	
		Итого		**177,66**	

Ведомость вырезов и закладных в потолке


Марка	Устройство	Кол.	Пом.
	Светильник встраиваемый (марки — план освещения)	30	1, 2, 3, 5, 6, 8
	Светильник накладной (марки — план освещения)	7	4, 7, 9, 10, 11, 12
	Светильник подвесной (марки — план освещения)	1	5
ИП2, ИП1, ИП6, ИП3, ИП12	Извещатель дымовой	5	2, 5, 6, 8, 9
ИП4	Извещатель тепловой	1	1
АР1	Точка доступа Wi-Fi, PoE	1	8
ВР2	Решётка вытяжная (вентилятор)	1	3
	Люк ревизии 300×300	3	1, 2, 5

Примечания

1. За отметку ±0,000 принят уровень чистого пола сухих помещений 1-го этажа (готовое покрытие), а не существующего пола; пол пом. 3, 11, 12 — −0,015, −0,030; существующий пол снимается до плиты, его отметка не замерена. Отметки в прямоугольниках — низ потолка, низ перекрытия +2,800. Марка потолка — одна конструкция и отметка на весь альбом.
2. Размеры помещений в свету (ширина × длина, мм), не поместившиеся на плане: пом. 2 — 2880 × 4140; пом. 3 — 2940 × 540, 2880 × 1140; пом. 5 — 5940 × 3680; пом. 6 — 2880 × 3480; пом. 9 — 1680 × 2080; пом. 12 — 1740 × 1940.
3. Потолки ГКЛ — каркасная система П113: подвесы через 1000 (с запасом: СП 163, табл. 14 — до 1100 при 0,15 кН/м²), несущие профили через 500, основные через 1200 мм; листы — поперёк несущих профилей. В помещениях 3 — ГКЛВ на оцинкованном каркасе.
4. Нижний уровень — пояс-короб по периметру шириной 300 мм (карниз подсветки + 150 мм полки), верхний — поле внутри пояса: пом. 5.
5. LED-лента в алюминиевом профиле посередине карниза короба шириной 300 мм (узел 1, лист 50); длина по плану: пом. 5 — 21,1 м (в плане освещения 21,1).
6. Балки декоративные 150×120 мм, фальш-балка, массив лиственницы под маслом: пом. 5 — 4 шт., 20,8 м; пом. 6 — 2 шт., 3,8 м, низ +2,580; крепление — на закладной брус 50×50 к каркасу П113, саморезы скрыто.
7. Ниши под шторы 150×100 мм — на всю длину стены с окном; карниз — на закладной до обшивки (узел 2 — пом. 1, 2, лист 50; узел 3 — пом. 5, лист 51).
8. Примыкание к стенам: теневой шов 15 мм, техзазор 3 мм — пом. 2, 5, по стенам, выровненным штукатуркой (узел 1); пом. 1, 3, 6, 8 — разделительная лента.
9. Светильники и потолочные устройства — подложка с планов освещения, слаботочных систем и вентиляции (положение — по ним); вырезы и закладные — по ведомости на листе, до обшивки; отверстия не совмещать с профилями, глубина корпуса светильника до 70 мм.
10. Разрезы 1–1 — лист 50; 3–3, 4–4 — лист 51; высоты мебели и дверных блоков сверены с низом потолка в разрезах; гибка бортов фигур и ленты ниш — там же; размеры фигурных уровней фрагменты 1 (лист 52); 2 (лист 53).
11. Шпаклевание ГКЛ и условия приёмки — Q3: рассеянный дневной свет, осмотр с 2 м; боковой свет не оценивается.
12. Пом. 1: короб воздуховода кухонной вытяжки ГКЛ 300×200 мм (ширина от стены × высота), низ +2,600, длина 2,86 м — по трассе плана вентиляции, вдоль стен до входа в канал под воздуховод Ø125; каркас ПН 28×27 по стене и плите, ПП 60×27, лист ГКЛ 12,5.
13. Люки ревизии 300×300 мм — по центру блоков питания LED (БП3, БП4, БП1; координаты — план освещения).
14. Пом. 6: над маршем лестницы Л-1 — проём перекрытия 1000×3100 мм; потолок ГКЛ по кромке проёма закрыт бортом до перекрытия (ГКЛ по ПН 28×27, длина кромки 5,1 м); светильники и устройства в проёме не ставятся.
15. ПТ0а — пом. 4, 7, 9, 10: потолок под покраску, без подвесного потолка, низ +2,800; материал и цвет — по ведомости отделки.
16. ПТ0б — пом. 11, 12: потолок под покраску (летнее помещение), без подвесного потолка, низ +2,800; материал и цвет — по ведомости отделки.
17. Основание потолка ПТ0а, ПТ0б — по проекту КР дома: конструкция перекрытия в исходных данных не задана.
18. Сечения потолков М 1:10: пом. 1 — 1.1, 1.2, 1.3 (лист 54); пом. 2 — 2.1, 2.2, 2.3 (лист 54).

					Проект: Дом 331 м² — **М 1:75**
	Лист	№ док.	Подпись	Дата	План потолков · 1-й этаж
Дизайнер	Кырлан А.С.			04.11.26	

Стадия	Лист	Листов
П	48	168

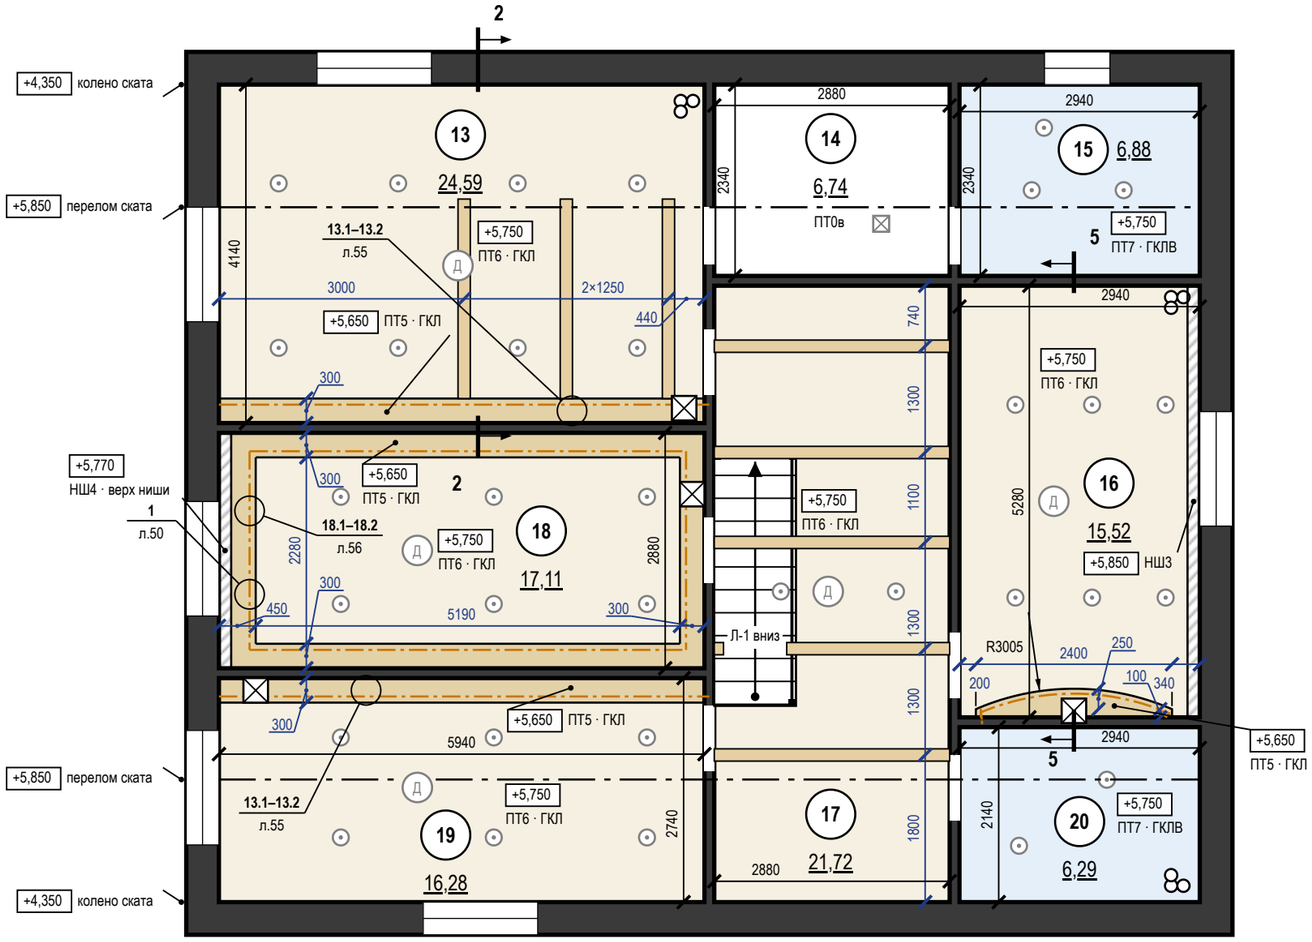

Ведомость потолков

Пом.	Марка	Конструкция	Низ / верх ниши	S, м²	Q
13	ПТ5	ГКЛ П113, короб LED	+5,650	1,78	Q3
13	ПТ6	ГКЛ П113	+5,750	22,81	Q3
14	ПТ0в	Обшивка скатов и горизонтальной части мансарды (конструкция — по проекту КР), окраска	+5,850	6,74	
15	ПТ7	ГКЛВ П113	+5,750	6,88	Q3
16	ПТ5	ГКЛ П113, дуга + LED	+5,650	0,64	Q3
16	ПТ6	ГКЛ П113	+5,750	14,09	Q3
16	НШ3	ниша под шторы 150×100	+5,850	0,79	
17	ПТ6	ГКЛ П113	+5,750	21,72	Q3
18	ПТ5	ГКЛ П113, короб LED	+5,650	4,84	Q3
18	ПТ6	ГКЛ П113	+5,750	11,84	Q3
18	НШ4	ниша под шторы 150×120	+5,770	0,43	
19	ПТ5	ГКЛ П113, короб LED	+5,650	1,78	Q3
19	ПТ6	ГКЛ П113	+5,750	14,50	Q3
20	ПТ7	ГКЛВ П113	+5,750	6,29	Q3
		Итого		**115,13**	


Примечания

1. За отметку ±0,000 принят уровень чистого пола 1-го этажа (готовое покрытие), а не существующего пола; чистый пол сухих помещений этажа — +3,150; пол пом. 15, 20 — +3,135; верх плиты перекрытия +3,086 — расчётный по пирогу пола, не замерен; существующий пол снимается до плиты, его отметка не замерена. Отметки в прямоугольниках — низ потолка. Марка потолка — одна конструкция и отметка на весь альбом.
2. Размеры помещений в свету (ширина × длина, мм), не поместившиеся на плане: пом. 13 — 5940 × 4140; пом. 17 — 2880 × 7540; пом. 18 — 5940 × 2880.
3. Мансарда: потолок по скатам кровли — от +4,350 у наружных стен вдоль конька до +5,850 у линий перелома (штрихпунктир), между ними — горизонтальная часть +5,850 (в пом. 13, 15, 16, 17, 18, 19, 20 горизонтальная часть подшита ниже — по марке и отметке потолка; скат обшит до линии подшивки); над слуховыми окнами скат поднят до горизонтальной части. Обшивка скатов — по стропилам с пароизоляцией по проекту КР.
4. Потолки ГКЛ — каркасная система П113: подвесы через 1000 (с запасом: СП 163, табл. 14 — до 1100 при 0,15 кН/м²), несущие профили через 500, основные через 1200 мм; листы — поперёк несущих профилей. В помещениях 15, 20 — ГКЛВ на оцинкованном каркасе.
5. Нижний уровень — пояс-короб по периметру шириной 300 мм (карниз подсветки + 150 мм полки), верхний — поле внутри пояса: пом. 18.
6. Короб-полоса у одной стены (не по периметру): ПТ5 шириной 300 мм — пом. 13 у стены В, пом. 19 у стены А.
7. LED-лента в алюминиевом профиле посередине карниза короба шириной 300 мм (узел 1, лист 50); длина по плану: пом. 13 — 6,0 м (в плане освещения 6); пом. 18 — 15,5 м (в плане освещения 15,5); пом. 19 — 6,0 м (в плане освещения 6).
8. Балки декоративные 150×120 мм, фальш-балка, массив лиственницы под маслом: пом. 13 — 3 шт., 7,3 м; пом. 17 — 5 шт., 14,4 м, низ +5,630; крепление — на закладной брус 50×50 к каркасу П113, саморезы скрыто.
9. Ниши под шторы 150×100 мм — на всю длину стены с окном; карниз — на закладной до обшивки (узел 2 — пом. 16, лист 50; узел 3 — пом. 18, лист 51).
10. Примыкание к стенам: теневой шов 15 мм, техзазор 3 мм — пом. 16, 18, по стенам, выровненным штукатуркой (узел 1); пом. 13, 15, 17, 19, 20 — разделительная лента.
11. Светильники и потолочные устройства — подложка с планов освещения, слаботочных систем и вентиляции (положение — по ним); вырезы и закладные — по ведомости на листе, до обшивки; отверстия не совмещать с профилями, глубина корпуса светильника до 70 мм.
12. Разрезы 2–2 — лист 50; 5–5 — лист 52; высоты мебели и дверных блоков сверены с низом потолка в разрезах; гибка бортов фигур и ленты ниш — там же; размеры фигурных уровней — фрагмент 3 (лист 53).
13. Шпаклевание ГКЛ и условия приёмки — Q3: рассеянный дневной свет, осмотр с 2 м; боковой свет не оценивается.
14. Ведомость вырезов и закладных в потолке (Мансарда) — на листе 52; вырезы и закладные — до обшивки.
15. Люки ревизии 300×300 мм — по центру блоков питания LED (БП6, БП7, БП8, БП9; координаты — план освещения).
16. ПТ0в — пом. 14: обшивка скатов и горизонтальной части мансарды (конструкция — по проекту КР), окраска, низ горизонтальной части +5,850; материал и цвет — по ведомости отделки.
17. Сечения потолков М 1:10: пом. 16 — 16.1, 16.2, 16.3 (листы 55, 56).

					Проект: Дом 331 м² — М 1:75
	Лист	№ док.	Подпись	Дата	
Дизайнер	Кырлан А.С.			04.11.26	План потолков · Мансарда
					Стадия: П; Лист: 49; Листов: 168


Разрез 1–1 (М 1:40)

Пом. 5 Гостиная

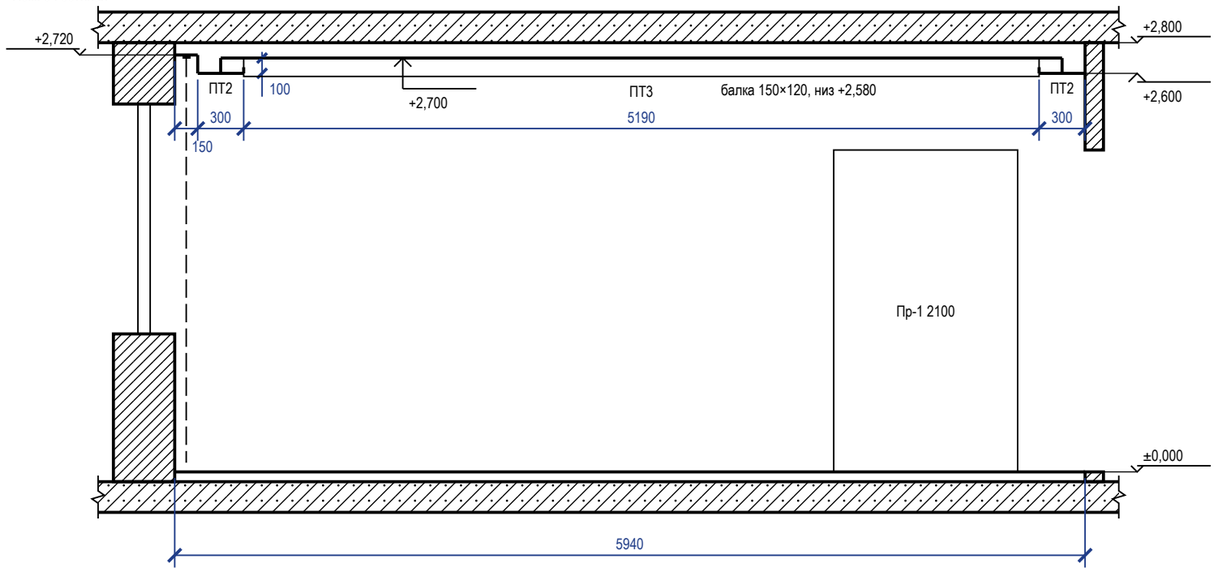


Разрез 2–2 (М 1:40)

Пом. 13 Спальня мастер (мансарда, потолок по скату)

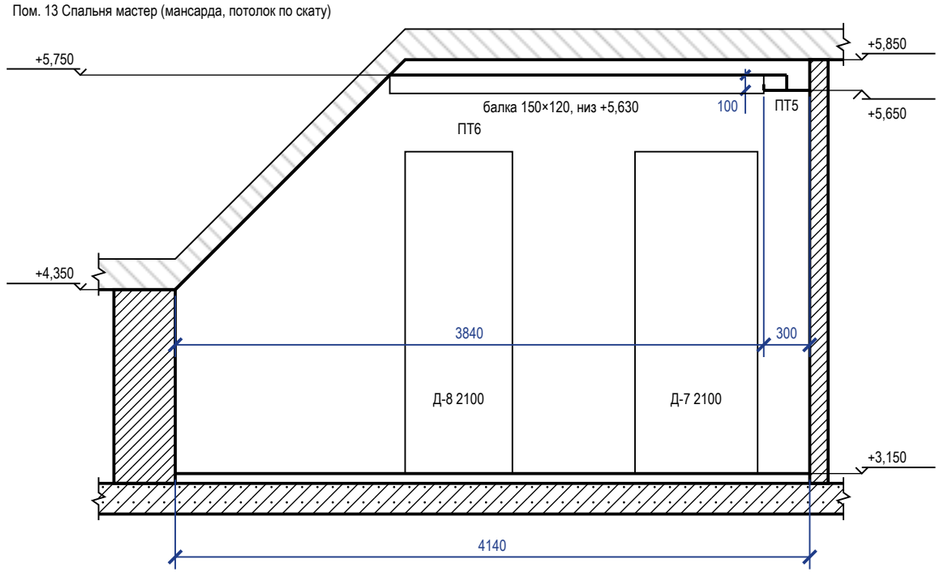

1 Короб с LED-подсветкой, теневой шов (М 1:10)

Пом. 5, 13, 18, 19; карниз 150×100, щель под свет 60 мм

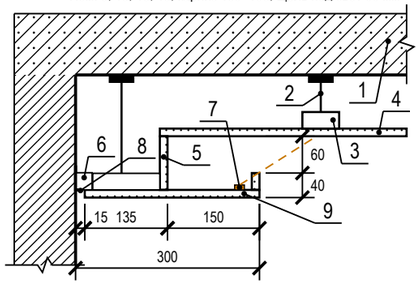


1 — плита перекрытия
2 — подвес прямой, шаг 1000 мм
3 — ПП 60×27: несущие через 500, основные через 1200 мм
4 — ГКЛ 12,5 по П113 — верхний уровень
5 — задняя стенка и бортик карниза — ГКЛ 12,5
6 — ПН 28×27 по периметру, к стене через 500 мм
7 — LED-лента в алюминиевом профиле
8 — теневой профиль: шов 15 мм, зазор 3 мм — пом. 5, 18; пом. 13, 19 — разделительная лента
9 — низ короба — ГКЛ 12,5 по ПП 60×27

Отметки по помещениям, м

Пом.	низ короба	верх. уровень	низ перекрытия
5	+2,600	+2,700	+2,800
13, 18, 19	+5,650	+5,750	+5,850

2 Ниша под шторы (М 1:10)

Пом. 1, 2, 16; без подсветки; закладные под карниз — до обшивки

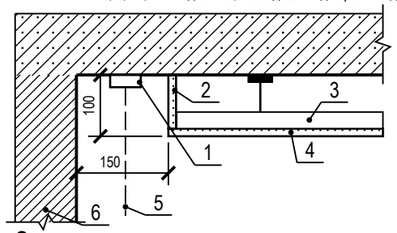

1 — карниз (шина), высота с верхом портьеры 100 мм
2 — стенка ниши — ГКЛ 12,5
3 — ПП 60×27 — каркас короба
4 — низ короба нижнего уровня — ГКЛ 12,5
5 — портьера
6 — стена с окном

Отметки по помещениям, м

Пом.	низ потолка	верх ниши	низ перекрытия
1, 2	+2,700	+2,800	+2,800
16	+5,750	+5,850	+5,850

Условные обозначения

- плита перекрытия в сечении
- стена в сечении
- потолок ГКЛ в сечении; под линией — марка потолка (план потолков)
- мебель и дверные проёмы за секущей плоскостью; число — марка и верх от чистого пола, мм
- портьера в нише под шторы
- балка декоративная: в сечении — заливка, за плоскостью — тонкой линией; низ балки — подписью у балки или отметкой справа
- кровля над мансардой (условно, по проекту КР)

Примечания

1. Разрезы — по линиям 1–1, 2–2 на плане потолков. Отметки — от ±0,000 (чистый пол 1-го этажа), м; размеры — мм.
2. Высоты мебели и дверных блоков за секущей плоскостью сверены с низом потолка над ними: верх ниже низа короба и поля.
3. ГКЛ 12,5 мм по каркасу П113; перепад уровней и бортик карниза — ГКЛ по ПП 60×27 (узел 1 — на этом листе). Ниша под шторы — на всю длину стены с окном, карниз на закладной до обшивки (узел 2 — на этом листе; узел 3 — лист 51).
4. Толщины плит перекрытия и пирога пола показаны условно.
5. Сечения потолков по помещениям М 1:10 (отметки помещения, профили, подвесы, крепёж, изделия) — листы 54–56.
6. Ведомость объёмов потолков (лист ГКЛ, профиль, подвесы, лента, блоки питания, люки) — на листе 53.
7. Фрагменты 1, 3, 2 — помещения с фигурными уровнями (размеры фигур, радиусы, отметки) — на листах 52, 53.


					Проект: Дом 331 м² — М 1:40; 1:10
	Лист	№ док.	Подпись	Дата	
Дизайнер	Кырлан А.С.			04.11.26	Разрезы и узлы потолков

Стадия	Лист	Листов
П	50	168

выпуск 04.11.2026 № f163a372b2 · стр. 50 из 168


Разрез 3–3 (М 1:40)

Пом. 1 Кухня-столовая

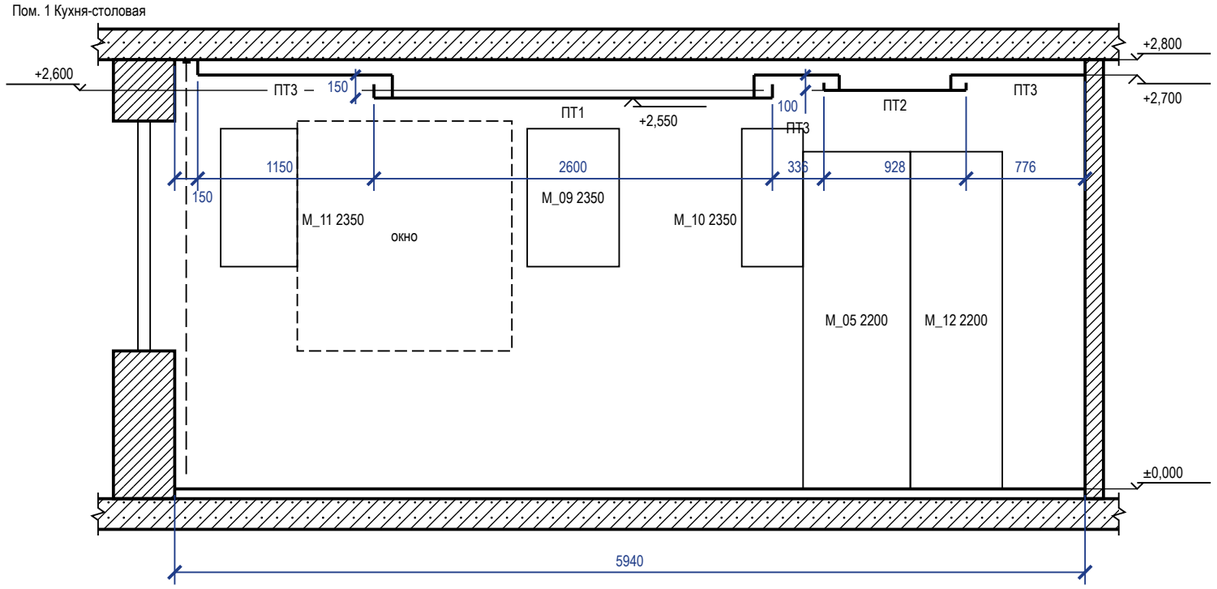


Разрез 4–4 (М 1:40)

Пом. 2 Кабинет-гостевая

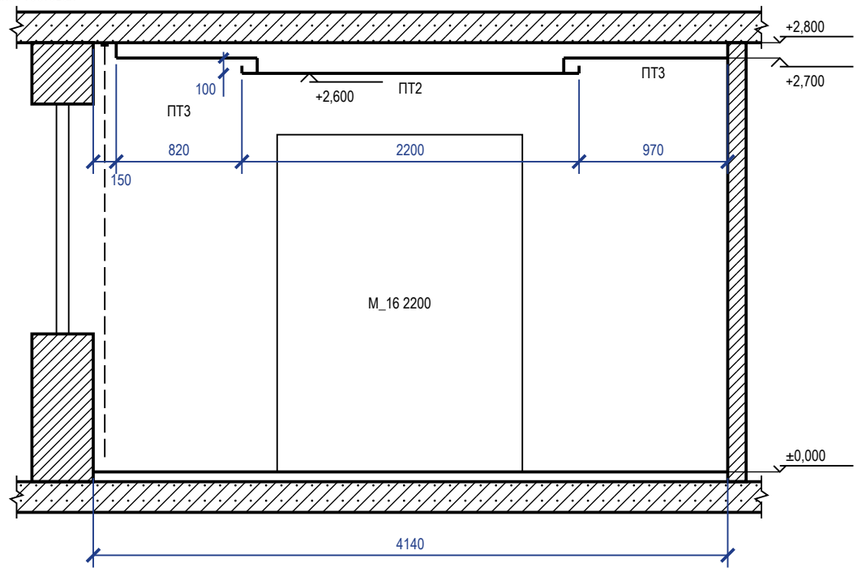

3 Ниша под шторы (М 1:10)


Пом. 5, 18; без подсветки; закладные под карниз — до обшивки

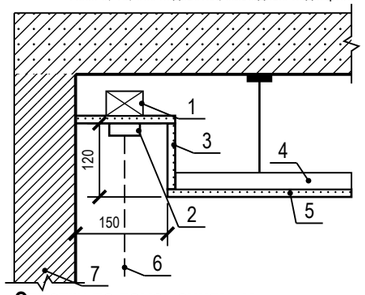

1 — закладная под карниз — брус 40×50
2 — карниз (шина), высота с верхом портьеры 100 мм
3 — стенка и потолок ниши — ГКЛ 12,5
4 — ПП 60×27 — каркас короба
5 — низ короба нижнего уровня — ГКЛ 12,5
6 — портьера
7 — стена с окном

4 Ниша LED фигурного уровня (М 1:10)

Пом. 1; карниз 120×100, щель под свет 60 мм

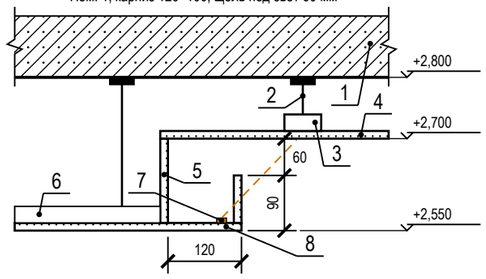

1 — плита перекрытия
2 — подвес прямой, шаг 1000 мм
3 — ПП 60×27: несущие через 500, основные через 1200 мм
4 — ГКЛ 12,5 по П113 — верхний уровень
5 — задняя стенка и бортик карниза — ГКЛ 12,5
6 — ПП 60×27 каркаса нижнего уровня, ПН по контуру фигуры (на дуге — с надрезами)
7 — LED-лента в алюминиевом профиле
8 — низ короба — ГКЛ 12,5 по ПП 60×27

Условные обозначения

- плита перекрытия в сечении
- стена в сечении
- потолок ГКЛ в сечении; под линией — марка потолка (план потолков)
- мебель и дверные проёмы за секущей плоскостью; число марка и верх от чистого пола, мм
- портьера в нише под шторы
- LED-лента в нише подсветки (карниз короба, ниша фигуры)

Отметки по помещениям, м

Пом.	низ потолка	верх ниши	низ перекрытия
5	+2,600	+2,720	+2,800
18	+5,650	+5,770	+5,850

Примечания


1. Разрезы — по линиям 3–3, 4–4 на плане потолков. Отметки — от ±0,000 (чистый пол 1-го этажа), м; размеры — мм.
2. Высоты мебели и дверных блоков за секущей плоскостью сверены с низом потолка над ними: верх ниже низа короба и поля.
3. ГКЛ 12,5 мм по каркасу П113; узлы коробов и ниш под шторы: узел 1 — лист 50; узел 2 — лист 50; узел 3 — на этом листе.
4. Толщины плит перекрытия и пирога пола показаны условно.

					Проект: Дом 331 м² — М 1:40; 1:10
	Лист	№ док.	Подпись	Дата	
Дизайнер	Кырлан А.С.			04.11.26	Разрезы и узлы потолков (продолжение)

Стадия	Лист	Листов
П	51	168


Разрез 5–5 (М 1:40)

Пом. 16 Спальня 2 (мансарда, разрез по горизонтальной части)

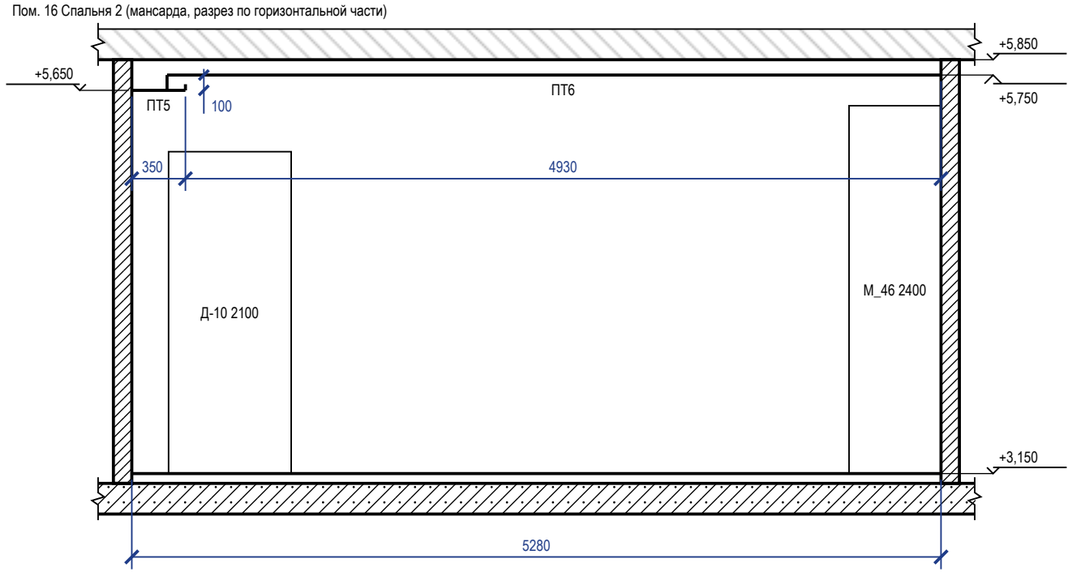

Фрагмент 1. Пом. 1 Кухня-столовая — уровни потолка (М 1:50)

Цепочки — от чистых граней стен; отметки — низ уровня от ±0,000

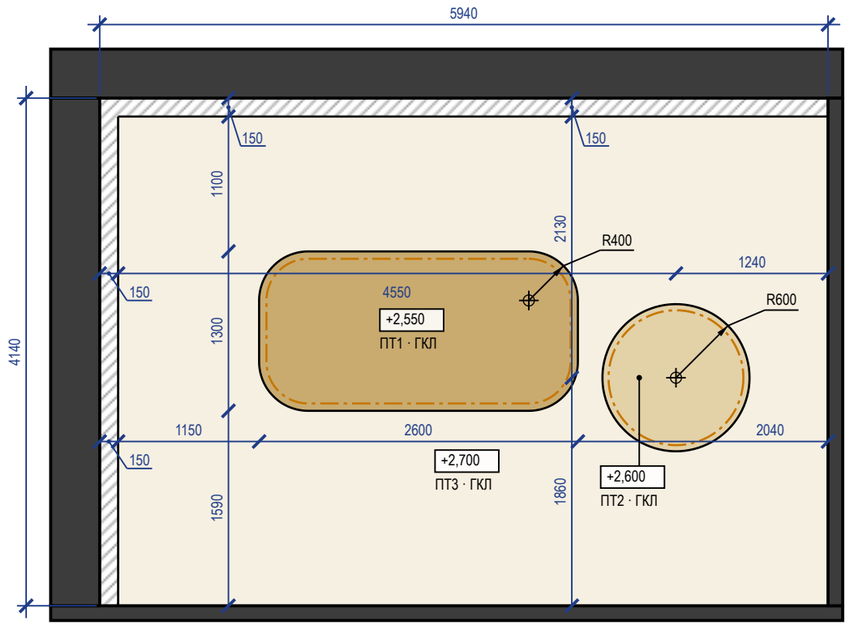


ПТ1 — низ +2,550 · ПТ2 — низ +2,600 · ПТ3 — низ +2,700

LED-лента в нише подсветки (карниз короба, ниша фигуры) · ниша под шторы

5 Ниша LED фигурного уровня (М 1:10)


Пом. 16; карниз 120×100, щель под свет 60 мм

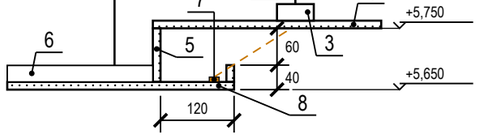

1 — плита перекрытия
2 — подвес прямой, шаг 1000 мм
3 — ПП 60×27: несущие через 500, основные через 1200 мм
4 — ГКЛ 12,5 по П113 — верхний уровень
5 — задняя стенка и бортик карниза — ГКЛ 12,5
6 — ПП 60×27 каркаса нижнего уровня, ПН по контуру фигуры (на дуге — с надрезами)
7 — LED-лента в алюминиевом профиле
8 — низ короба — ГКЛ 12,5 по ПП 60×27

6 Ниша LED фигурного уровня (М 1:10)

Пом. 2; карниз 100×100, щель под свет 50 мм

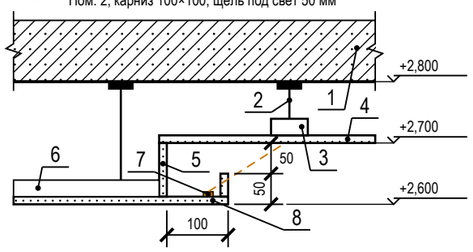

1 — плита перекрытия
2 — подвес прямой, шаг 1000 мм
3 — ПП 60×27: несущие через 500, основные через 1200 мм
4 — ГКЛ 12,5 по П113 — верхний уровень
5 — задняя стенка и бортик карниза — ГКЛ 12,5
6 — ПП 60×27 каркаса нижнего уровня, ПН по контуру фигуры (на дуге — с надрезами)
7 — LED-лента в алюминиевом профиле
8 — низ короба — ГКЛ 12,5 по ПП 60×27

Примечания

1. Разрезы — по линиям 5–5 на плане потолков. Отметки — от ±0,000 (чистый пол 1-го этажа), м; размеры — мм.
2. Высоты мебели и дверных блоков за секущей плоскостью сверены с низом потолка над ними: верх ниже низа короба и поля.
3. ГКЛ 12,5 мм по каркасу П113; узлы коробов и ниш под шторы: узел 1 — лист 50; узел 2 — лист 50; узел 3 — лист 51; условные обозначения разрезов — на листе 50.
4. Толщины плит перекрытия и пирога пола показаны условно.
5. Фрагмент 1 — фигурные уровни потолка крупно: привязки краёв и центров фигур к чистым граням стен, радиусы (R) с центрами, хорда и стрелка дуги, отметки низа каждого уровня; цвета уровней — как на плане потолков.
6. Фигурные уровни: борт — ГКЛ по ПН с надрезами (на дуге шаг стоек борта 300 мм при R до 2500, 400 — до 5000) или по гнутому заводскому профилю (СП 163, 6.3.3); гибка: остров пом. 1 R400 — ГКЛ 6,5 мокрой гибкой; круг пом. 1 R600 — ГКЛ 6,5 мокрой гибкой; эллипс пом. 2 R445 — ГКЛ 6,5 мокрой гибкой; дуга пом. 16 R3005 — ГКЛ 12,5 сухой гибкой (СП 163, табл. 9). Лента в нише фигуры по оси: остров пом. 1 — 6,7 м, круг пом. 1 — 3,5 м, эллипс пом. 2 — 5,4 м, дуга пом. 16 — 3,2 м; узел ниши LED фигуры: узел 4 — лист 51 — пом. 1; узел 6 — на этом листе — пом. 2; узел 5 — на этом листе пом. 16.

	Лист	№ док.	Подпись	Дата
Дизайнер	Кырлан А.С.			04.11.26

Проект: Дом 331 м² — **М 1:40; 1:50; 1:10**

Разрезы и узлы потолков (продолжение)


Стадия	Лист	Листов
П	52	168

Ведомость объёмов потолков

Позиция	Ед.	Кол.	Пом.
Лист ГКЛ 12,5	м²	205,77	1, 2, 5, 6, 8, 13, 16, 17, 18, 19
Лист ГКЛВ 12,5	м²	18,04	3, 15, 20
Лист ГКЛ арочный 6,5	м²	4,06	1, 2
Борта и карнизы (входят в площади листов выше)	м²	22,93	1, 2, 5, 6, 13, 16, 18, 19
Профиль ПП 60×27	м	601,81	1, 2, 3, 5, 6, 8, 13, 15, 16, 17, 18, 19, 20
Профиль ПН 28×27	м	474,23	1, 2, 3, 5, 6, 8, 13, 15, 16, 17, 18, 19, 20
Подвес прямой	шт.	226	1, 2, 3, 5, 6, 8, 13, 15, 16, 17, 18, 19, 20
Анкер-клин к плите	шт.	226	1, 2, 3, 5, 6, 8, 13, 15, 16, 17, 18, 19, 20
Шуруп TN 3,5×25	шт.	5194	1, 2, 3, 5, 6, 8, 13, 15, 16, 17, 18, 19, 20
Лента армирующая для швов	м	271,01	1, 2, 3, 5, 6, 8, 13, 15, 16, 17, 18, 19, 20
Шпаклёвка для швов	кг	90,34	1, 2, 3, 5, 6, 8, 13, 15, 16, 17, 18, 19, 20
Грунтовка (швы)	л	22,58	1, 2, 3, 5, 6, 8, 13, 15, 16, 17, 18, 19, 20
Лента разделительная по периметру	м	209,80	1, 2, 3, 5, 6, 8, 13, 15, 16, 17, 18, 19, 20
Сплошная шпаклёвка и окраска (площадь развёртки)	м²	225,84	1, 2, 3, 5, 6, 8, 13, 15, 16, 17, 18, 19, 20
Лента LED	м	67,45	1, 2, 5, 13, 16, 18, 19
Требуемая мощность блоков питания	Вт	842	1, 2, 5, 13, 16, 18, 19
Установленная мощность блоков питания	Вт	1450	1, 2, 5, 13, 16, 18, 19
Блок питания LED	шт.	7	1, 2, 5, 13, 16, 18, 19
Люк ревизии	шт.	7	1, 2, 5, 13, 16, 18, 19

Фрагмент 3. Пом. 16 Спальня 2 — уровни потолка (М 1:50)

Цепочки — от чистых граней стен; отметки — низ уровня от ±0,000

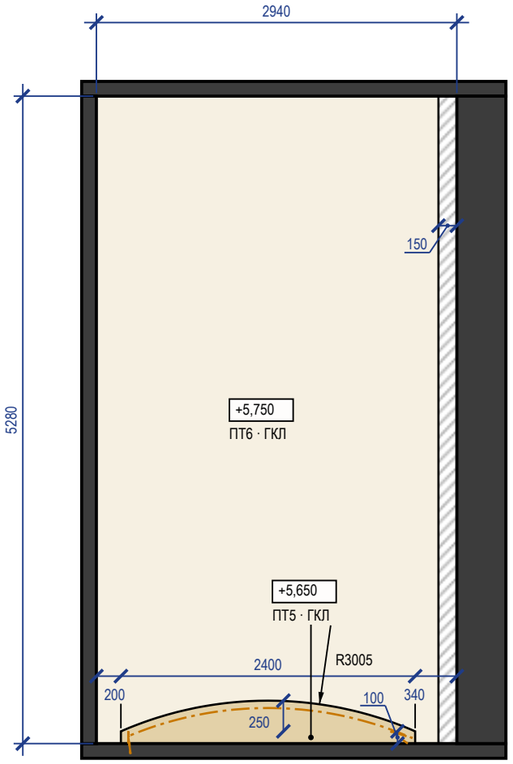


ПТ5 — низ +5,650 ПТ6 — низ +5,750

LED-лента в нише подсветки (карниз короба, ниша фигуры)

ниша под шторы

Фрагмент 2. Пом. 2 Кабинет-гостевая — уровни потолка (М 1:50)

Цепочки — от чистых граней стен; отметки — низ уровня от ±0,000

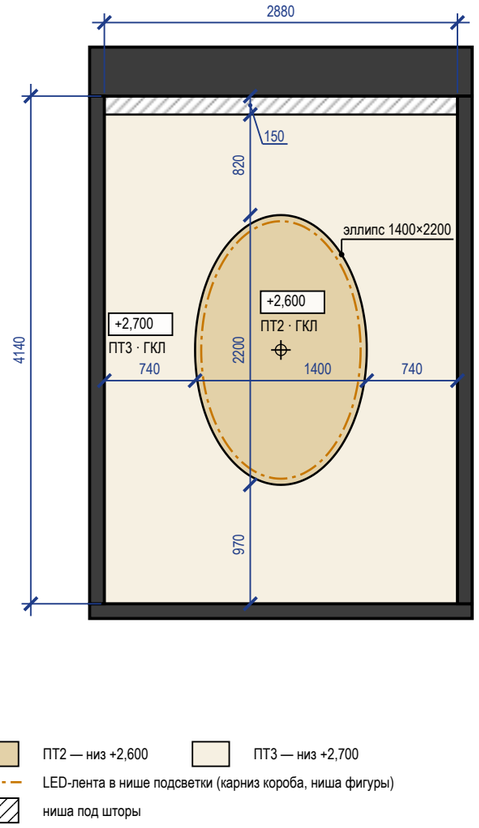

ПТ2 — низ +2,600 ПТ3 — низ +2,700

LED-лента в нише подсветки (карниз короба, ниша фигуры)

ниша под шторы

Примечания


1. ГКЛ 12,5 мм по каркасу П113; узлы коробов и ниш под шторы: узел 1 — лист 50; узел 2 — лист 50; узел 3 — лист 51; условные обозначения разрезов — на листе 50.
2. Фрагменты 3, 2 — фигурные уровни потолка крупно: привязки краёв и центров фигур к чистым граням стен, радиусы (R) с центрами, хорда и стрелка дуги, отметки низа каждого уровня; цвета уровней как на плане потолков.
3. Ведомость объёмов — по геометрии плана потолков: Лист ГКЛ 12,5 — плоскости уровней + борта (без арочных участков); Лист ГКЛВ 12,5 — плоскости уровней + борта; Лист ГКЛ арочный 6,5 — кривая борта × высота борта и стенки ниши × 2 слоя (R400 мокрая гибка, R600 мокрая гибка, R445 мокрая гибка); Борта и карнизы — длина перепада × перепад; Профиль ПП 60×27 — S × (1/шаг несущ. + 1/шаг осн.) + стойки бортов; Профиль ПН 28×27 — периметр стен + 2 × перепады + карнизы; Подвес прямой — по раскладке: S уровня / (шаг осн. × шаг подвесов), пояс уже шага — ряд вдоль пояса, фигура — по контуру; шаг подвесов — не больше табл. 14 СП 163; Анкер-клин к плите — по одному на подвес (Knauf П113); Шуруп TN 3,5×25 — 23 шт./м² (Knauf П113, табл. 2 альбома П 11); Лента армирующая для швов — 1,2 м/м² листа (Knauf); Шпаклёвка для швов — 0,4 кг/м² листа, только швы (Knauf); Грунтовка (швы) — 0,1 л/м² листа, только швы (Knauf); Лента разделительная по периметру — периметр стен под потолком ГКЛ; Сплошная шпаклёвка и окраска (площадь развёртки) — плоскости + борта; расход — по паспорту материала (норма расхода на сплошной слой не подтверждена); Лента LED — по оси карниза и ниши фигуры (план потолков); Требуемая мощность блоков питания — Вт/м × длина × 1,3; Установленная мощность блоков питания — сумма мощностей блоков по плану освещения; Блок питания LED — блоки потолочных лент по плану освещения (БП3, БП4, БП1, БП6, БП7, БП8, БП9); Люк ревизии — план потолков; без запаса на подрезку (при закупке листа: ×1,075 при S > 20 м², ×1,175 — 10–20 м², ×1,275 — < 10 м²).

					Проект: Дом 331 м² — **М 1:50**
	Лист	№ док.	Подпись	Дата	Разрезы и узлы потолков (продолжение)
Дизайнер	Кырлан А.С.			04.11.26	

Стадия	Лист	Листов
П	53	168

Сечение 1.1. Ниша LED фигурного уровня (М 1:10)


Пом. 1 Кухня-столовая; карниз 120×100, щель под свет 60 мм

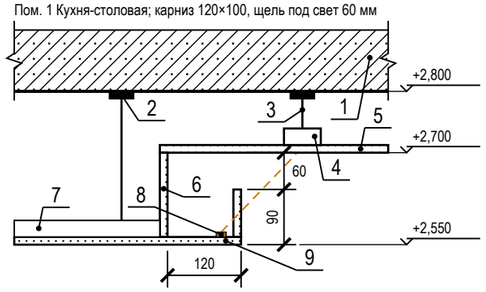

1 — плита перекрытия
2 — анкер-клин к плите — по одному на подвес
3 — подвес прямой, шаг 1000 мм
4 — ПП 60×27: несущие через 500, основные через 1200 мм; соединители одноуровневые, шурупы LN 3,5×9
5 — ГКЛ 12,5 по П113 — верхний уровень; шурупы TN 3,5×25 через 170 мм
6 — задняя стенка и бортик карниза — ГКЛ 12,5
7 — ПП 60×27 каркаса нижнего уровня, ПН по контуру фигуры (на дуге — с надрезами)
8 — LED-лента 9,6 Вт/м, 24 В в алюминиевом профиле
9 — низ короба — ГКЛ 12,5 по ПП 60×27

Сечение 1.2. Ниша под шторы (М 1:10)


Пом. 1 Кухня-столовая; без подсветки; закладные под карниз — до обшивки

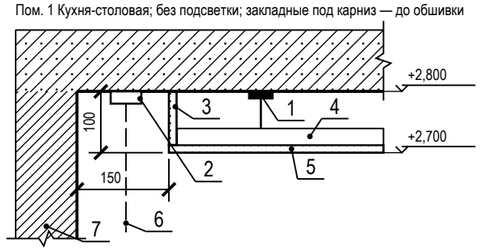

1 — анкер-клин к плите — по одному на подвес; подвес прямой, шаг 1000 мм
2 — карниз (шина), высота с верхом портьеры 100 мм
3 — стенка ниши — ГКЛ 12,5
4 — ПП 60×27 — каркас короба, основные через 1200 мм; соединители одноуровневые, шурупы LN 3,5×9
5 — низ короба нижнего уровня — ГКЛ 12,5; шурупы TN 3,5×25 через 170 мм
6 — портьера
7 — стена с окном

Сечение 1.3. Примыкание потолка к стене (М 1:10)


Пом. 1 Кухня-столовая; примыкание — разделительная лента

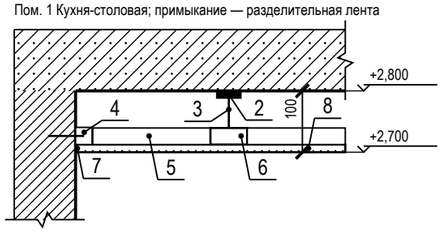

1 — плита перекрытия
2 — анкер-клин к плите — по одному на подвес
3 — подвес прямой, шаг 1000 мм
4 — ПН 28×27 по периметру — дюбель-гвоздь через ≤ 500 мм, не менее 3 на профиль
5 — ПП 60×27 несущий (вид) через 500 мм, в ПН
6 — ПП 60×27 основной (сечение) через 1200 мм; соединители одноуровневые, шурупы LN 3,5×9
7 — лента разделительная по стене, шов зашпаклёван
8 — ГКЛ 12,5 по П113; шурупы TN 3,5×25 через 170 мм

Сечение 2.1. Ниша LED фигурного уровня (М 1:10)


Пом. 2 Кабинет-гостевая; карниз 100×100, щель под свет 50 мм

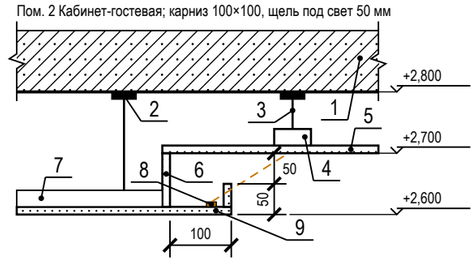

1 — плита перекрытия
2 — анкер-клин к плите — по одному на подвес
3 — подвес прямой, шаг 1000 мм
4 — ПП 60×27: несущие через 500, основные через 1200 мм; соединители одноуровневые, шурупы LN 3,5×9
5 — ГКЛ 12,5 по П113 — верхний уровень; шурупы TN 3,5×25 через 170 мм
6 — задняя стенка и бортик карниза — ГКЛ 12,5
7 — ПП 60×27 каркаса нижнего уровня, ПН по контуру фигуры (на дуге — с надрезами)
8 — LED-лента 9,6 Вт/м, 24 В в алюминиевом профиле
9 — низ короба — ГКЛ 12,5 по ПП 60×27

Сечение 2.2. Ниша под шторы (М 1:10)


Пом. 2 Кабинет-гостевая; без подсветки; закладные под карниз — до обшивки

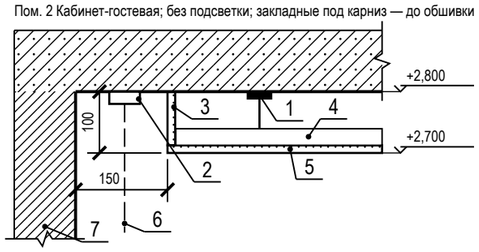

1 — анкер-клин к плите — по одному на подвес; подвес прямой, шаг 1000 мм
2 — карниз (шина), высота с верхом портьеры 100 мм
3 — стенка ниши — ГКЛ 12,5
4 — ПП 60×27 — каркас короба, основные через 1200 мм; соединители одноуровневые, шурупы LN 3,5×9
5 — низ короба нижнего уровня — ГКЛ 12,5; шурупы TN 3,5×25 через 170 мм
6 — портьера
7 — стена с окном

Сечение 2.3. Примыкание потолка к стене (М 1:10)

Пом. 2 Кабинет-гостевая; примыкание — теневой шов

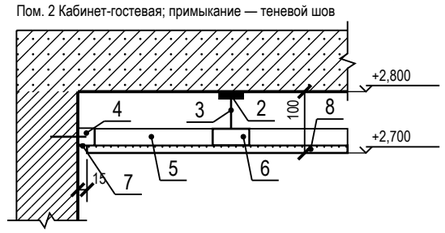

1 — плита перекрытия
2 — анкер-клин к плите — по одному на подвес
3 — подвес прямой, шаг 1000 мм
4 — ПН 28×27 по периметру — дюбель-гвоздь через ≤ 500 мм, не менее 3 на профиль
5 — ПП 60×27 несущий (вид) через 500 мм, в ПН
6 — ПП 60×27 основной (сечение) через 1200 мм; соединители одноуровневые, шурупы LN 3,5×9
7 — теневой профиль: шов 15 мм, зазор 3 мм; стена под шов выровнена
8 — ГКЛ 12,5 по П113; шурупы TN 3,5×25 через 170 мм

Условные обозначения

— · — LED-лента в нише подсветки (карниз короба, ниша фигуры)


Примечания

1. Сечения потолков М 1:10 по помещениям с нишами LED и нишами под шторы: отметки и размеры этого помещения от ±0,000 — чистого пола 1-го этажа (м, мм). Положение — по плану потолков (листы 48, 49): короб и ниша LED — по линиям ленты, ниша под шторы — у стены с окном; типовые узлы по группам помещений — на листе 50.
2. Крепёж: подвес прямой к плите на анкер-клине — по одному на подвес (Knauf П113); ПН к стенам — дюбель-гвоздь через ≤ 500 мм, не менее 3 на профиль (серия 1.045.9-2.08); лист 12,5 — шурупы TN 3,5×25 через 170 мм (СП 163, табл. 15); профили между собой — соединители одноуровневые, шурупы LN 3,5×9.
3. Изделие карниза, профиля LED и галтели подписано артикулом из данных; где артикул не выбран, сечение дано по габаритам из данных (ширина и глубина ниши, щель под свет), изделие подбирается по ним.

					Проект: Дом 331 м²	М 1:10
	Лист	№ док.	Подпись	Дата		
Дизайнер	Кырлан А.С.			04.11.26	Сечения потолков М 1:10	Стадия: П; Лист: 54; Листов: 168

Сечение 5.1. Короб с LED-подсветкой, теневой шов (М 1:10)


Пом. 5 Гостиная; карниз 150×100, щель под свет 60 мм

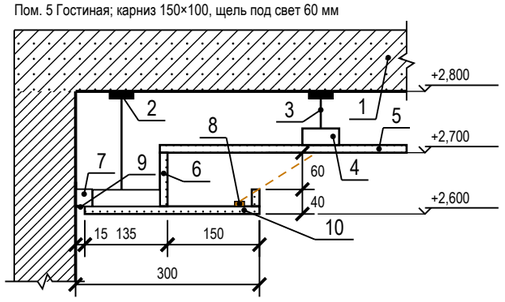

1 — плита перекрытия
2 — анкер-клин к плите — по одному на подвес
3 — подвес прямой, шаг 1000 мм
4 — ПП 60×27: несущие через 500, основные через 1200 мм; соединители одноуровневые, шурупы LN 3,5×9
5 — ГКЛ 12,5 по П113 — верхний уровень; шурупы TN 3,5×25 через 170 мм
6 — задняя стенка и бортик карниза — ГКЛ 12,5
7 — ПН 28×27 по периметру — дюбель-гвоздь через ≤ 500 мм, не менее 3 на профиль
8 — LED-лента 9,6 Вт/м, 24 В в алюминиевом профиле
9 — теневой профиль: шов 15 мм, зазор 3 мм
10 — низ короба — ГКЛ 12,5 по ПП 60×27

Сечение 5.2. Ниша под шторы (М 1:10)


Пом. 5 Гостиная; без подсветки; закладные под карниз — до обшивки

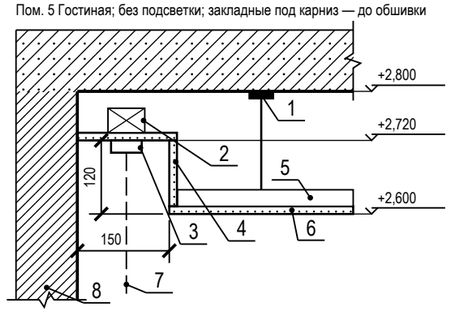

1 — анкер-клин к плите — по одному на подвес; подвес прямой, шаг 1000 мм
2 — закладная под карниз — брус 40×50
3 — карниз (шина), высота с верхом портьеры 100 мм
4 — стенка и потолок ниши — ГКЛ 12,5
5 — ПП 60×27 — каркас короба, основные через 1200 мм; соединители одноуровневые, шурупы LN 3,5×9
6 — низ короба нижнего уровня — ГКЛ 12,5; шурупы TN 3,5×25 через 170 мм
7 — портьера
8 — стена с окном

Сечение 13.1. Короб с LED-подсветкой (М 1:10)


Пом. 13 Спальня мастер, 19 Спальня 4; карниз 150×100, щель под свет 60 мм

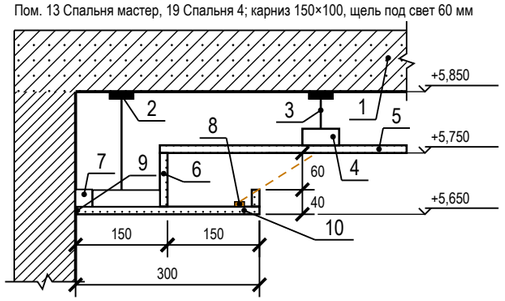

1 — плита перекрытия
2 — анкер-клин к плите — по одному на подвес
3 — подвес прямой, шаг 1000 мм
4 — ПП 60×27: несущие через 500, основные через 1200 мм; соединители одноуровневые, шурупы LN 3,5×9
5 — ГКЛ 12,5 по П113 — верхний уровень; шурупы TN 3,5×25 через 170 мм
6 — задняя стенка и бортик карниза — ГКЛ 12,5
7 — ПН 28×27 по периметру — дюбель-гвоздь через ≤ 500 мм, не менее 3 на профиль
8 — LED-лента 9,6 Вт/м, 24 В в алюминиевом профиле
9 — примыкание к стене — лента разделительная, шов зашпаклёван
10 — низ короба — ГКЛ 12,5 по ПП 60×27

Сечение 13.2. Примыкание потолка к стене (М 1:10)


Пом. 13 Спальня мастер, 19 Спальня 4; примыкание — разделительная лента

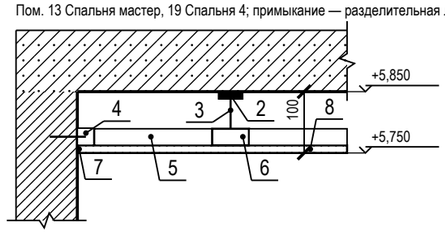

1 — плита перекрытия
2 — анкер-клин к плите — по одному на подвес
3 — подвес прямой, шаг 1000 мм
4 — ПН 28×27 по периметру — дюбель-гвоздь через ≤ 500 мм, не менее 3 на профиль
5 — ПП 60×27 несущий (вид) через 500 мм, в ПН
6 — ПП 60×27 основной (сечение) через 1200 мм; соединители одноуровневые, шурупы LN 3,5×9
7 — лента разделительная по стене, шов зашпаклёван
8 — ГКЛ 12,5 по П113; шурупы TN 3,5×25 через 170 мм

Сечение 16.1. Ниша LED фигурного уровня (М 1:10)


Пом. 16 Спальня 2; карниз 120×100, щель под свет 60 мм

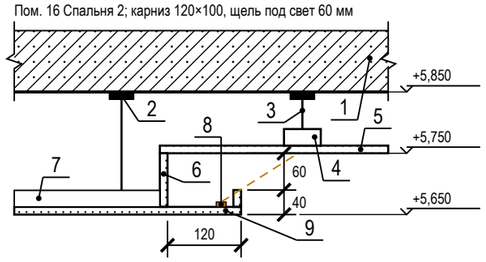

1 — плита перекрытия
2 — анкер-клин к плите — по одному на подвес
3 — подвес прямой, шаг 1000 мм
4 — ПП 60×27: несущие через 500, основные через 1200 мм; соединители одноуровневые, шурупы LN 3,5×9
5 — ГКЛ 12,5 по П113 — верхний уровень; шурупы TN 3,5×25 через 170 мм
6 — задняя стенка и бортик карниза — ГКЛ 12,5
7 — ПП 60×27 каркаса нижнего уровня, ПН по контуру фигуры (на дуге — с надрезами)
8 — LED-лента 9,6 Вт/м, 24 В в алюминиевом профиле
9 — низ короба — ГКЛ 12,5 по ПП 60×27

Сечение 16.2. Ниша под шторы (М 1:10)

Пом. 16 Спальня 2; без подсветки; закладные под карниз — до обшивки

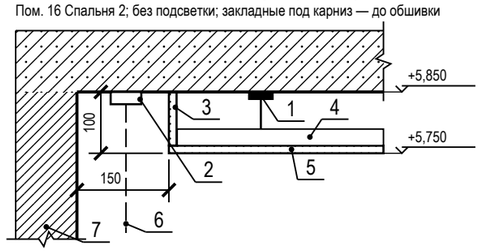

1 — анкер-клин к плите — по одному на подвес; подвес прямой, шаг 1000 мм
2 — карниз (шина), высота с верхом портьеры 100 мм
3 — стенка ниши — ГКЛ 12,5
4 — ПП 60×27 — каркас короба, основные через 1200 мм; соединители одноуровневые, шурупы LN 3,5×9
5 — низ короба нижнего уровня — ГКЛ 12,5; шурупы TN 3,5×25 через 170 мм
6 — портьера
7 — стена с окном

Условные обозначения

LED-лента в нише подсветки (карниз короба, ниша фигуры)


Примечания

1. Сечения потолков М 1:10 по помещениям с нишами LED и нишами под шторы: отметки и размеры этого помещения от ±0,000 — чистого пола 1-го этажа (м, мм). Положение — по плану потолков (листы 48, 49): короб и ниша LED — по линиям ленты, ниша под шторы — у стены с окном; типовые узлы по группам помещений — на листе 50.
2. Крепёж: подвес прямой к плите на анкер-клине — по одному на подвес (Knauf П113); ПН к стенам — дюбель-гвоздь через ≤ 500 мм, не менее 3 на профиль (серия 1.045.9-2.08); лист 12,5 — шурупы TN 3,5×25 через 170 мм (СП 163, табл. 15); профили между собой — соединители одноуровневые, шурупы LN 3,5×9.
3. Изделие карниза, профиля LED и галтели подписано артикулом из данных; где артикул не выбран, сечение дано по габаритам из данных (ширина и глубина ниши, щель под свет), изделие подбирается по ним.

					Проект: Дом 331 м²	М 1:10
	Лист	№ док.	Подпись	Дата	Сечения потолков М 1:10	Стадия / Лист / Листов
Дизайнер	Кырлан А.С.			04.11.26		П / 55 / 168

Сечение 16.3. Примыкание потолка к стене (М 1:10)


Пом. 16 Спальня 2; примыкание — теневой шов

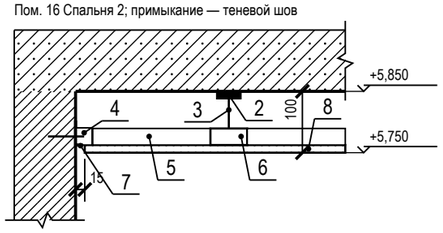

1 — плита перекрытия
2 — анкер-клин к плите — по одному на подвес
3 — подвес прямой, шаг 1000 мм
4 — ПН 28×27 по периметру — дюбель-гвоздь через ≤ 500 мм, не менее 3 на профиль
5 — ПП 60×27 несущий (вид) через 500 мм, в ПН
6 — ПП 60×27 основной (сечение) через 1200 мм; соединители одноуровневые, шурупы LN 3,5×9
7 — теневой профиль: шов 15 мм, зазор 3 мм; стена под шов выровнена
8 — ГКЛ 12,5 по П113; шурупы TN 3,5×25 через 170 мм

Сечение 18.1. Короб с LED-подсветкой, теневой шов (М 1:10)


Пом. 18 Спальня 3; карниз 150×100, щель под свет 60 мм

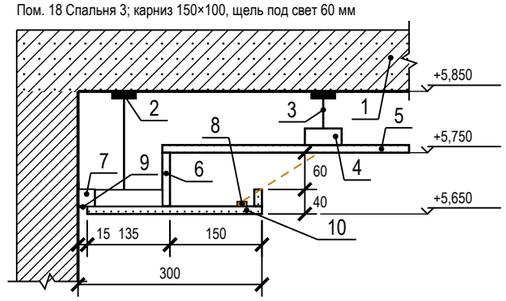

1 — плита перекрытия
2 — анкер-клин к плите — по одному на подвес
3 — подвес прямой, шаг 1000 мм
4 — ПП 60×27: несущие через 500, основные через 1200 мм; соединители одноуровневые, шурупы LN 3,5×9
5 — ГКЛ 12,5 по П113 — верхний уровень; шурупы TN 3,5×25 через 170 мм
6 — задняя стенка и бортик карниза — ГКЛ 12,5
7 — ПН 28×27 по периметру — дюбель-гвоздь через ≤ 500 мм, не менее 3 на профиль
8 — LED-лента 9,6 Вт/м, 24 В в алюминиевом профиле
9 — теневой профиль: шов 15 мм, зазор 3 мм
10 — низ короба — ГКЛ 12,5 по ПП 60×27

Сечение 18.2. Ниша под шторы (М 1:10)

Пом. 18 Спальня 3; без подсветки; закладные под карниз — до обшивки

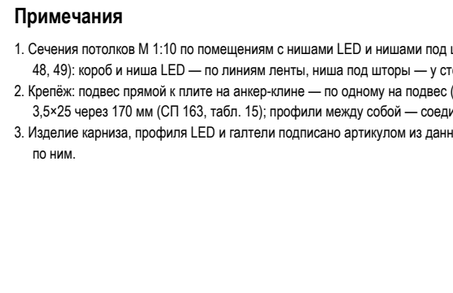

1 — анкер-клин к плите — по одному на подвес; подвес прямой, шаг 1000 мм
2 — закладная под карниз — брус 40×50
3 — карниз (шина), высота с верхом портьеры 100 мм
4 — стенка и потолок ниши — ГКЛ 12,5
5 — ПП 60×27 — каркас короба, основные через 1200 мм; соединители одноуровневые, шурупы LN 3,5×9
6 — низ короба нижнего уровня — ГКЛ 12,5; шурупы TN 3,5×25 через 170 мм
7 — портьера
8 — стена с окном

Условные обозначения

— · — LED-лента в нише подсветки (карниз короба, ниша фигуры)


Примечания

1. Сечения потолков М 1:10 по помещениям с нишами LED и нишами под шторы: отметки и размеры этого помещения от ±0,000 — чистого пола 1-го этажа (м, мм). Положение — по плану потолков (листы 48, 49): короб и ниша LED — по линиям ленты, ниша под шторы — у стены с окном; типовые узлы по группам помещений — на листе 50.
2. Крепёж: подвес прямой к плите на анкер-клине — по одному на подвес (Knauf П113); ПН к стенам — дюбель-гвоздь через ≤ 500 мм, не менее 3 на профиль (серия 1.045.9-2.08); лист 12,5 — шурупы TN 3,5×25 через 170 мм (СП 163, табл. 15); профили между собой — соединители одноуровневые, шурупы LN 3,5×9.
3. Изделие карниза, профиля LED и галтели подписано артикулом из данных; где артикул не выбран, сечение дано по габаритам из данных (ширина и глубина ниши, щель под свет), изделие подбирается по ним.

					Проект: Дом 331 м²	М 1:10
	Лист	№ док.	Подпись	Дата		
Дизайнер	Кырлан А.С.			04.11.26	Сечения потолков М 1:10	Стадия / Лист / Листов
						П / 56 / 168

Условные обозначения

- автоматический выключатель, QF — номер группы, характеристика и ток
- УЗО (с автоматом — дифавтомат): ток утечки, тип AC/A
- Wh — счётчик электроэнергии
- шина: L — фаза, N — нулевой рабочий, PE — защитный проводник
- УЗИП (ограничитель перенапряжений), FV — марка
- ГЗШ — главная заземляющая шина; штрихпунктир — проводник основной системы уравнивания потенциалов (ОСУП)
- обрыв шины: схема продолжена на следующем листе
- резервный аппарат (не менее 20 % групп)

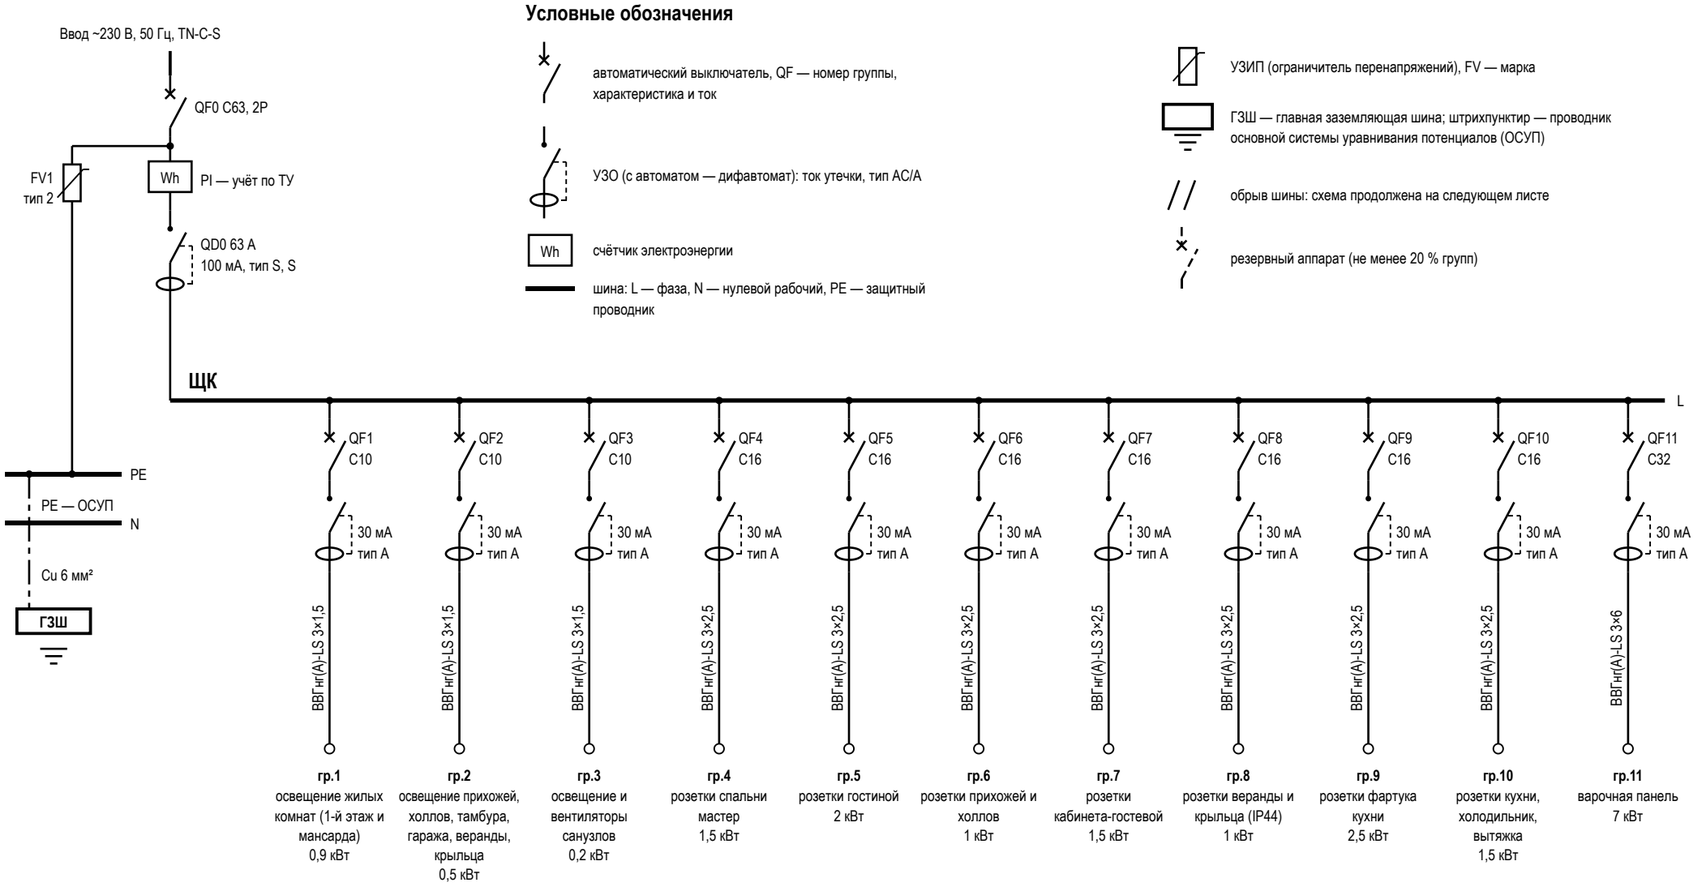

Данные щитка

Показатель	Значение
Номер щитка	ЩК
Тип	ЩРВ-П-72, IP41
Уст. мощность, кВт	36,1
Разреш. мощность, кВт	15
Расчётная, кВт	13,8
Автоматы 1п: занят. / рез.	21 / 5
Модулей: всего / занято	72 / 48
Ток на вводе, А	63
Вводной аппарат	QF0 C63, 2P
УЗИП	FV1, тип 2, ЩК, после счётчика
ГЗШ, проводник ОСУП	Cu 6 мм²
Листов схемы	2 (группы по листам)

Таблица групп щита ЩК и кабельный журнал

№	Назначение	Помещения	Автомат	УЗО / дифавтомат	Кабель	Длина, м	Р, кВт	Точек
1	освещение жилых комнат (1-й этаж и мансарда)	1, 2, 5, 6, 7, 13, 14, 16, 17, 18, 19	C10	30 мА, тип A	ВВГнг(A)-LS 3×1,5	387,2	0,9	99
2	освещение прихожей, холлов, тамбура, гаража, веранды, крыльца	4, 5, 6, 8, 9, 10, 11, 12, 17	C10	30 мА, тип A	ВВГнг(A)-LS 3×1,5	157,7	0,5	27
3	освещение и вентиляторы санузлов	3, 6, 15, 17, 20	C10	30 мА, тип A	ВВГнг(A)-LS 3×1,5	84,7	0,2	17
4	розетки спальни мастер	13	C16	30 мА, тип A	ВВГнг(A)-LS 3×2,5	37,7	1,5	6
5	розетки гостиной	5	C16	30 мА, тип A	ВВГнг(A)-LS 3×2,5	33,5	2	6
6	розетки прихожей и холлов	6, 8, 17	C16	30 мА, тип A	ВВГнг(A)-LS 3×2,5	22	1	4
7	розетки кабинета-гостевой	2	C16	30 мА, тип A	ВВГнг(A)-LS 3×2,5	24,9	1,5	6
8	розетки веранды и крыльца (IP44)	11, 12	C16	30 мА, тип A	ВВГнг(A)-LS 3×2,5	35	1	2
9	розетки фартука кухни	1	C16	30 мА, тип A	ВВГнг(A)-LS 3×2,5	32,1	2,5	4
10	розетки кухни, холодильник, вытяжка	1	C16	30 мА, тип A	ВВГнг(A)-LS 3×2,5	33,6	1,5	6
11	варочная панель	1	C32	30 мА, тип A	ВВГнг(A)-LS 3×6	23,6	7	1

Примечания

1. Схема однолинейная: одна линия — фаза, N и PE группы; аппараты — в отключённом положении (ГОСТ 2.702, ГОСТ 2.755). Номера групп — как у точек на планах (гр.). За отметку 0,000 принят уровень чистого пола; высота щита — по плану розеток.
2. Розеточные и мокрые линии — через УЗО или дифавтомат с током утечки не более 30 мА (ПУЭ 7.1.79); в санузле выполнить ДСУП (ПУЭ 7.1.87–7.1.88).
3. УЗО тип A — для линий с электроникой, стиральной и посудомоечной машиной, LED-драйверами; тип AC — только для чисто активной нагрузки.
4. Кабель — медный, исполнение нг(A)-LS (ГОСТ 31565-2012); скрытая прокладка только горизонтально и вертикально, фактические трассы зафиксировать исполнительной схемой до закрытия отделкой.
5. Номинал автомата — не выше допустимого тока кабеля: 1,5 мм² — до 10 А, 2,5 мм² — до 16 А. Резерв щита — не менее 20 % модулей.
6. Расчёт нагрузок, токов КЗ, селективности и сечений — по проекту ЭОМ организации с допуском СРО; лист задаёт состав, расположение и группы.
7. УЗИП FV1 — после вводного автомата, проводник к шине PE — кратчайший, без петель. Шина PE щита соединяется с ГЗШ проводником ОСУП; к ГЗШ присоединяются трубы водопровода и отопления на вводе в квартиру (ПУЭ 7.1.87). Шины N и PE — раздельные, после разделения PEN не объединяются.
8. До подключения нагрузки — приёмо-сдаточные испытания с протоколом: сопротивление изоляции линий не менее 0,5 МОм, срабатывание УЗО по току и времени, непрерывность защитных проводников PE (ПУЭ, гл. 1.8).

					Проект: Дом 331 м²
	Лист	№ док.	Подпись	Дата	Однолинейная схема щита
Дизайнер	Кырлан А.С.			04.11.26	

Стадия	Лист	Листов
П	57	168

Продолжение однолинейной схемы щита ЩК, начало — лист 57

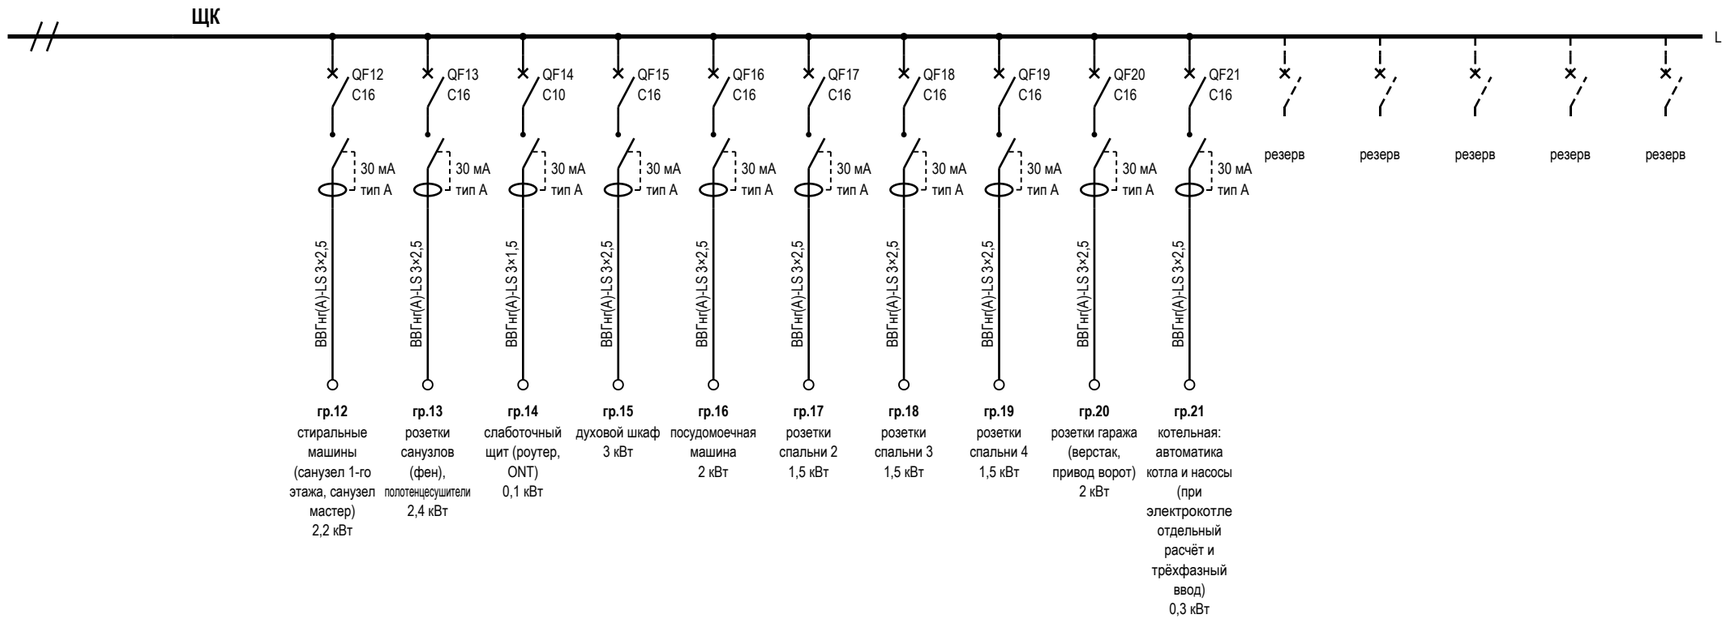


Таблица групп щита ЩК и кабельный журнал (продолжение)


№	Назначение	Помещения	Автомат	УЗО / дифавтомат	Кабель	Длина, м	Р, кВт	Точек
12	стиральные машины (санузел 1-го этажа, санузел мастер)	3, 15	C16	30 мА, тип А	ВВГнг(А)-LS 3×2,5	22,8	2,2	2
13	розетки санузлов (фен), полотенцесушители	3, 15, 20	C16	30 мА, тип А	ВВГнг(А)-LS 3×2,5	57,5	2,4	6
14	слаботочный щит (роутер, ONT)	8	C10	30 мА, тип А	ВВГнг(А)-LS 3×1,5	3,8	0,1	1
15	духовой шкаф	1	C16	30 мА, тип А	ВВГнг(А)-LS 3×2,5	22,7	3	1
16	посудомоечная машина	1	C16	30 мА, тип А	ВВГнг(А)-LS 3×2,5	16,2	2	1
17	розетки спальни 2	16	C16	30 мА, тип А	ВВГнг(А)-LS 3×2,5	25,7	1,5	6
18	розетки спальни 3	18	C16	30 мА, тип А	ВВГнг(А)-LS 3×2,5	29,7	1,5	6
19	розетки спальни 4	19	C16	30 мА, тип А	ВВГнг(А)-LS 3×2,5	29,8	1,5	6
20	розетки гаража (верстак, привод ворот)	10	C16	30 мА, тип А	ВВГнг(А)-LS 3×2,5	23,9	2	3
21	котельная: автоматика котла и насосы (при электрокотле отдельный расчёт и трёхфазный ввод)	4	C16	30 мА, тип А	ВВГнг(А)-LS 3×2,5	16,2	0,3	1
	Итого по сечениям ВВГнг(А)-LS (все группы щита), м: 3×1,5 — 633,4; 3×2,5 — 463,3; 3×6 — 23,6					1120,3		

Примечания

1. Лист — продолжение однолинейной схемы щита ЩК: начало, данные щитка и условные обозначения — лист 57. Ввод, учёт, вводной аппарат, УЗИП, шины N и PE и ГЗШ показаны там же; шина L листа — та же шина щита.
2. Схема однолинейная: одна линия — фаза, N и PE группы; аппараты — в отключённом положении (ГОСТ 2.702, ГОСТ 2.755). Номера групп — как у точек на планах (гр.). За отметку 0,000 принят уровень чистого пола; высота щита — по плану розеток.
3. Розеточные и мокрые линии — через УЗО или дифавтомат с током утечки не более 30 мА (ПУЭ 7.1.79); в санузле выполнить ДСУП (ПУЭ 7.1.87–7.1.88).
4. УЗО тип А — для линий с электроникой, стиральной и посудомоечной машиной, LED-драйверами; тип АС — только для чисто активной нагрузки.
5. Кабель — медный, исполнение нг(А)-LS (ГОСТ 31565-2012); скрытая прокладка только горизонтально и вертикально, фактические трассы зафиксировать исполнительной схемой до закрытия отделкой.
6. Номинал автомата — не выше допустимого тока кабеля: 1,5 мм² — до 10 А, 2,5 мм² — до 16 А. Резерв щита — не менее 20 % модулей.
7. Расчёт нагрузок, токов КЗ, селективности и сечений — по проекту ЭОМ организации с допуском СРО; лист задаёт состав, расположение и группы.
8. До подключения нагрузки — приёмо-сдаточные испытания с протоколом: сопротивление изоляции линий не менее 0,5 МОм, срабатывание УЗО по току и времени, непрерывность защитных проводников PE (ПУЭ, гл. 1.8).

					Проект: Дом 331 м²
	Лист	№ док.	Подпись	Дата	
Дизайнер	Кырлан А.С.			04.11.26	Однолинейная схема щита (продолжение)
					Стадия: П; Лист: 58; Листов: 168

выпуск 04.11.2026 № f163a372b2 · стр. 58 из 168

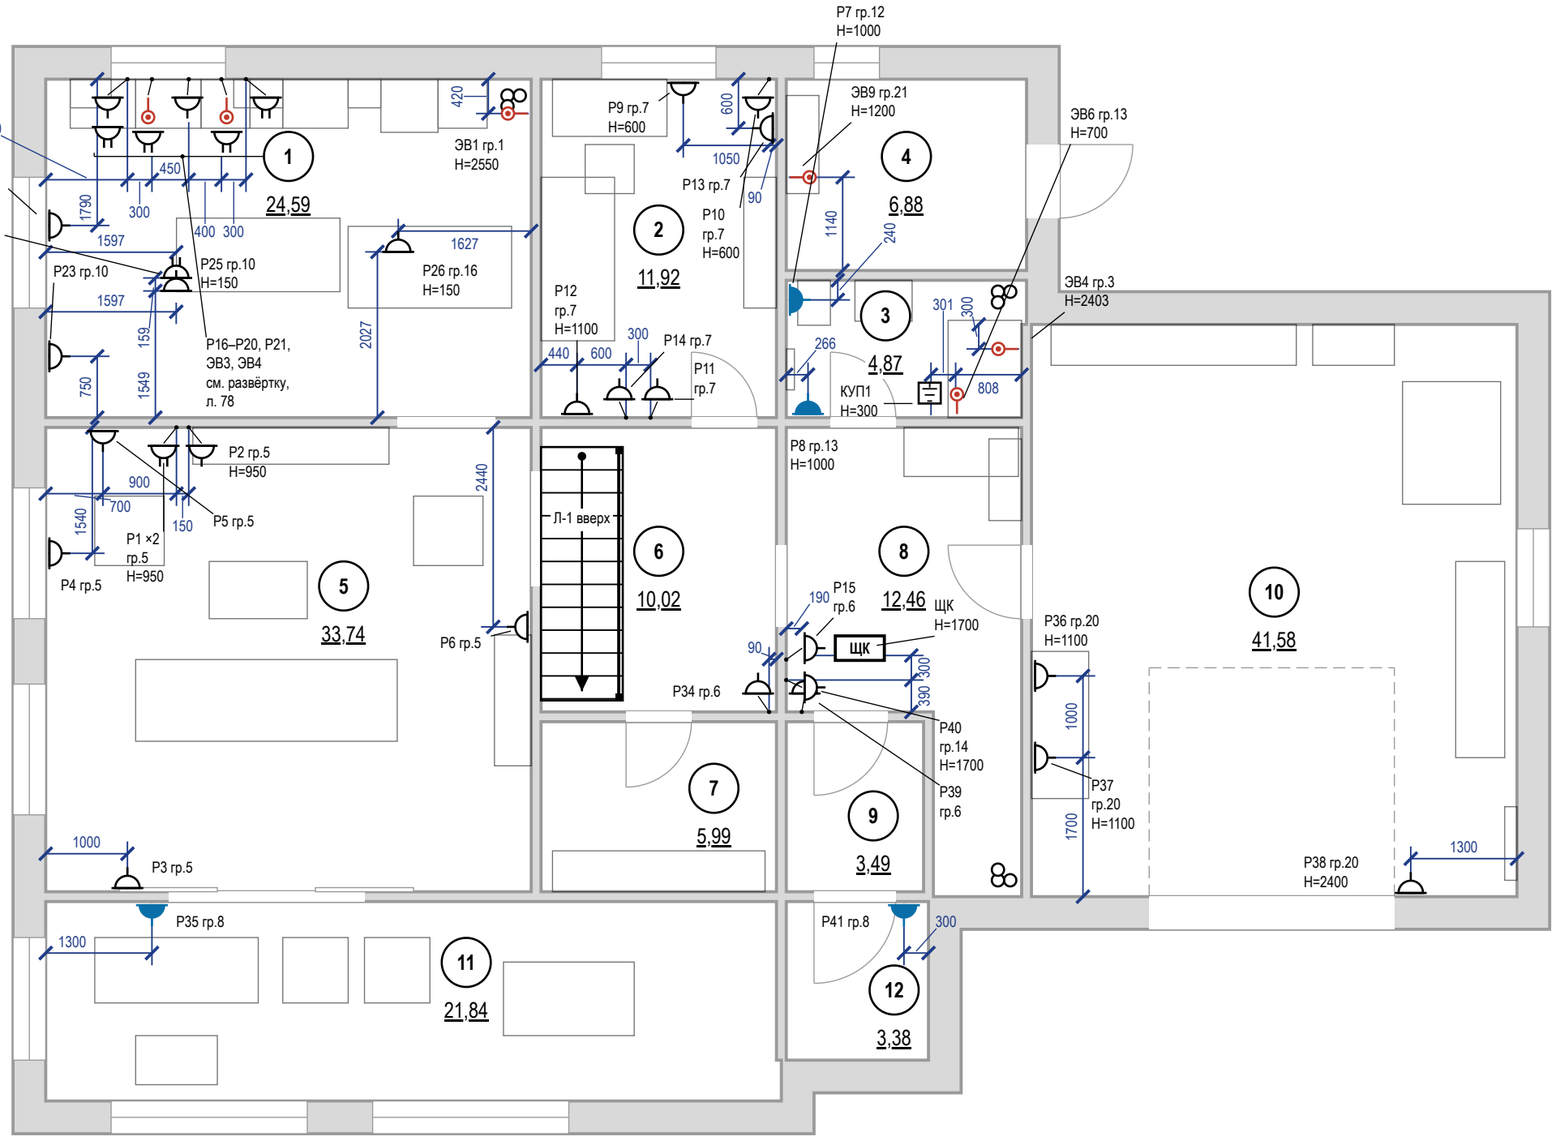

Условные обозначения

Знак	Тип изделия	Н, мм	Кол., шт
	Розетка с заземлением	300	12
	То же	у знака	12
	Блок розеток с заземлением, рамка 2 поста	у знака	6
	Розетка с заземлением IP44	300	2
	То же	у знака	2
	Вывод кабеля к прибору	у знака	6
	КУП (уравнивание потенциалов)	300	1
ЩК	Щит квартирный	1700	1

розетка с заземляющим контактом; у знака — марка, ×N — постов в рамке, гр. — группа щита, Н — высота оси, мм

знак разведён для читаемости: точка на стене — у выноски, привязка — до неё

мебель и сантехприборы — подложка

стояк: К1 — канализация, В1 — ХВС, Т3 — ГВС


1 — номер помещения, площадь м²

Итого розеток (механизмов) — 40 шт; рамок — 34 шт: на 1 пост — 28, на 2 поста — 6.

Примечания

1. За отметку 0,000 принят уровень чистого пола. Высоты Н — от чистого пола до оси изделия; привязки — от чистовой грани стены до оси механизма (у рамки на несколько постов — до оси рамки).
2. Розетки без отметки Н у знака — на высоте 300 мм от чистого пола до оси механизма; выводы кабеля — по паспорту прибора.
3. Розетки в санузле — только вне зон 0–2 (ПУЭ 7.1.48, ГОСТ Р 50571.7.701-2024), IP44, через УЗО 30 мА.
4. Розеточные и мокрые линии — через УЗО или дифавтомат с током утечки не более 30 мА (ПУЭ 7.1.79); в санузле выполнить ДСУП (ПУЭ 7.1.87–7.1.88).
5. Кабель — медный, исполнение нг(А)-LS (ГОСТ 31565-2012); скрытая прокладка только горизонтально и вертикально, фактические трассы зафиксировать исполнительной схемой до закрытия отделкой.
6. Расчёт нагрузок, токов КЗ, селективности и сечений — по проекту ЭОМ организации с допуском СРО; лист задаёт состав, расположение и группы.
7. Выводы кухонной техники — после утверждения проекта кухни (ориентировочно); привязки выводов даны от осей модулей гарнитура и пересматриваются вместе с проектом кухни.
8. Электрический тёплый пол проектом не предусмотрен; при решении заказчика устроить — отдельный лист «План тёплых полов»: контуры с отступом 100 мм от стен и мебели без ножек, датчик в гофре, терморегулятор, своя группа щита через УЗО 30 мА.

					Проект: Дом 331 м²	М 1:75
	Лист	№ док.	Подпись	Дата		
Дизайнер	Кырлан А.С.			04.11.26	План розеток и электровыводов · 1-й этаж	Стадия: П; Лист: 59; Листов: 168

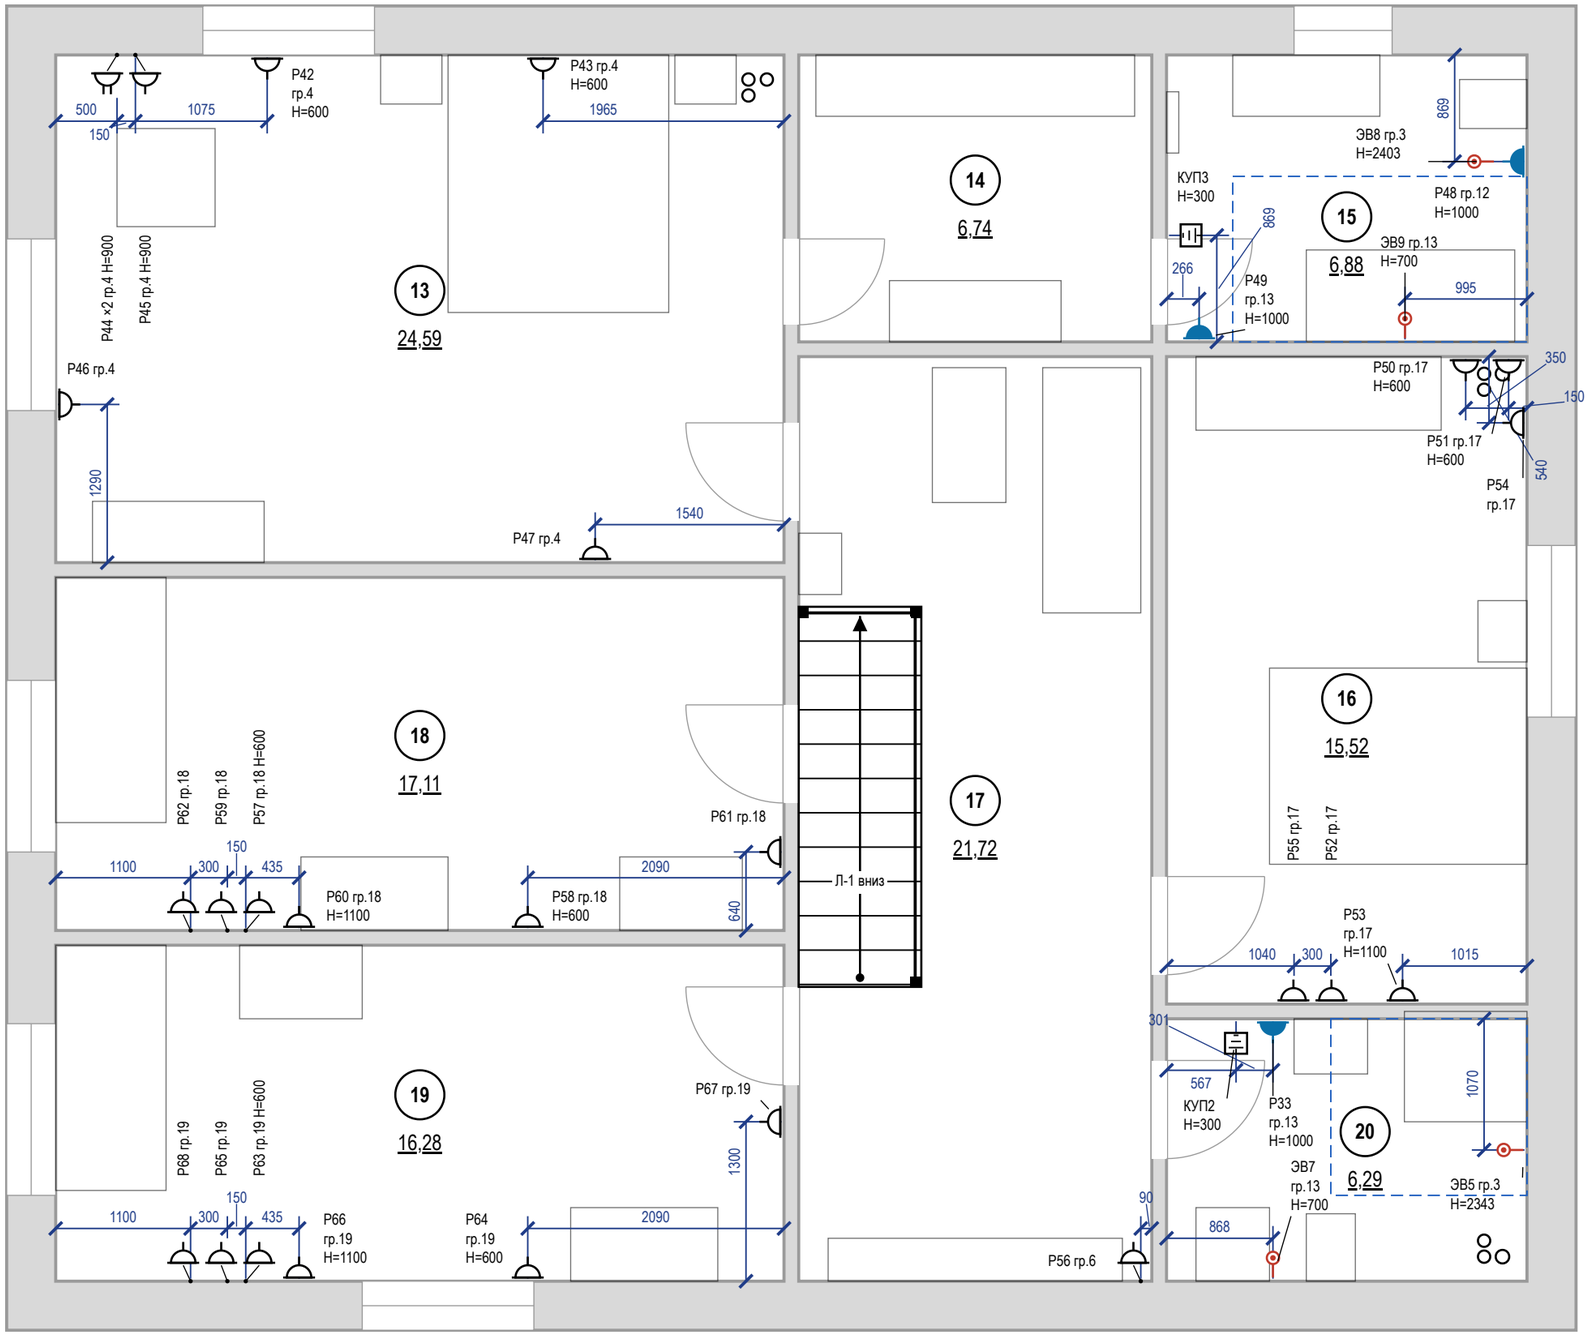

Условные обозначения

Знак	Тип изделия	Н, мм	Кол., шт
	Розетка с заземлением	300	12
	То же	у знака	12
	Блок розеток с заземлением, рамка 2 поста	900	1
	Розетка с заземлением IP44	1000	3
	Вывод кабеля к прибору	у знака	4
	КУП (уравнивание потенциалов)	300	2

розетка с заземляющим контактом; у знака — марка, ×N — постов в рамке, гр. — группа щита, Н — высота оси, мм

знак разведён для читаемости: точка на стене — у выноски, привязка — до неё

граница зоны 2 ванной (600 мм от ванны/поддона)

мебель и сантехприборы — подложка

стояк: К1 — канализация, В1 — ХВС, Т3 — ГВС

(1) номер помещения, площадь м²

Итого розеток (механизмов) — 29 шт; рамок — 28 шт: на 1 пост — 27, на 2 поста — 1.

Примечания


1. За отметку 0,000 принят уровень чистого пола. Высоты Н — от чистого пола до оси изделия; привязки — от чистовой грани стены до оси механизма (у рамки на несколько постов — до оси рамки).
2. Розетки без отметки Н у знака — на высоте 300 мм от чистого пола до оси механизма; выводы кабеля — по паспорту прибора.
3. Розетки в санузле — только вне зон 0–2 (ПУЭ 7.1.48, ГОСТ Р 50571.7.701-2024), IP44, через УЗО 30 мА.
4. Розеточные и мокрые линии — через УЗО или дифавтомат с током утечки не более 30 мА (ПУЭ 7.1.79); в санузле выполнить ДСУП (ПУЭ 7.1.87–7.1.88).
5. Кабель — медный, исполнение нг(А)-LS (ГОСТ 31565-2012); скрытая прокладка только горизонтально и вертикально, фактические трассы зафиксировать исполнительной схемой до закрытия отделкой.
6. Расчёт нагрузок, токов КЗ, селективности и сечений — по проекту ЭОМ организации с допуском СРО; лист задаёт состав, расположение и группы.
7. Электрический тёплый пол проектом не предусмотрен; при решении заказчика устроить — отдельный лист «План тёплых полов»: контуры с отступом 100 мм от стен и мебели без ножек, датчик в гофре, терморегулятор, своя группа щита через УЗО 30 мА.

	Лист	№ док.	Подпись	Дата
Дизайнер	Кырлан А.С.			04.11.26

Проект: Дом 331 м² — **М 1:50**

План розеток и электровыводов · Мансарда

Стадия	Лист	Листов
П	60	168

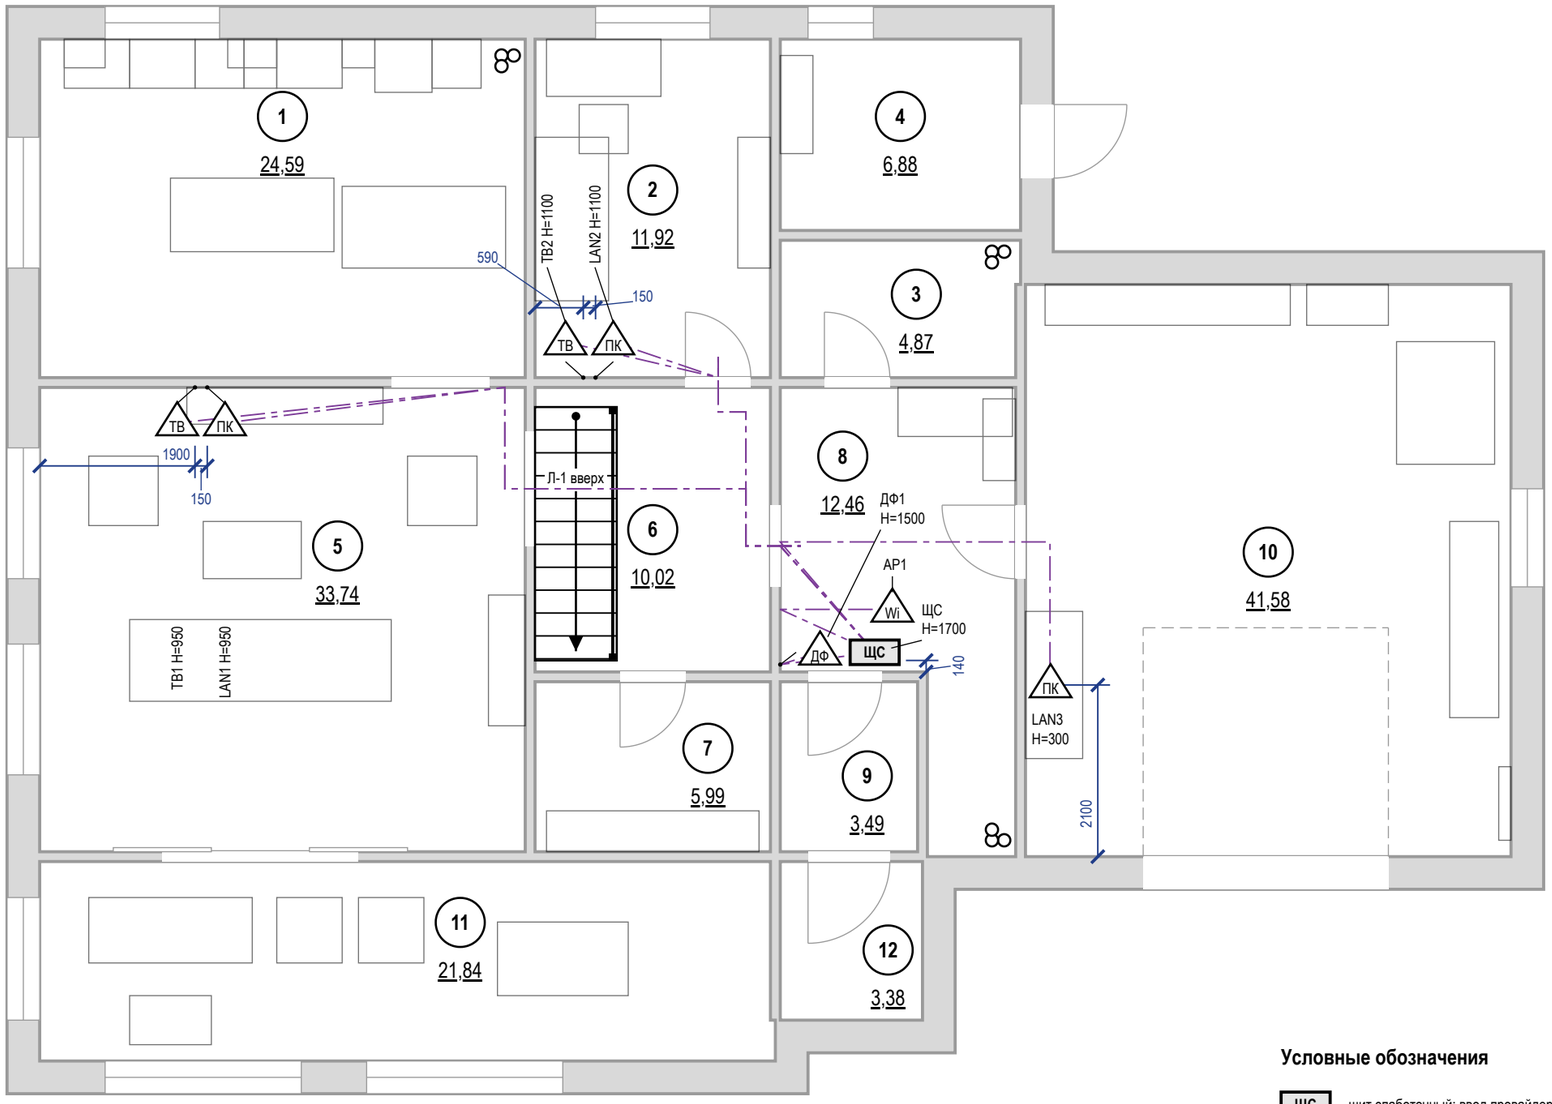


Условные обозначения

- ЩС — щит слаботочный: ввод провайдера, роутер, коммутатор
- ПК — розетка компьютерная RJ45
- ТВ — розетка телевизионная
- ДФ — трубка или монитор домофона
- Wi — точка доступа Wi-Fi (питание PoE)
- кабель от ЩС до точки, отдельным лучом
- мебель и сантехприборы — подложка
- стояк: К1 — канализация, В1 — ХВС, Т3 — ГВС
- 1 — номер помещения, площадь м²

Примечания

1. За отметку 0,000 принят уровень чистого пола. Высоты Н — от чистого пола до оси изделия; привязки — от чистовой грани стены до оси механизма (у рамки на несколько постов — до оси рамки).
2. Высота установки, не указанная на плане: розетки LAN и ТВ — 300 мм от чистого пола.
3. Слаботочные кабели — отдельно от силовых: в своей трубе или лотке, при параллельной прокладке не ближе 100 мм к силовым, пересечения под прямым углом; каждую точку — отдельным кабелем от ЩС без скруток.
4. Трассы на листе — принципиальные; фактические зафиксировать исполнительной схемой до закрытия отделкой. Силовые линии, УЗО 30 мА, ДСУП, кабель нг(A)-LS — по листам розеток и щита.
5. Проект силовой части и расчёт токов КЗ — по проекту ЭОМ; слаботочная часть согласуется с провайдером (ввод в дом, место ONT) и с заказчиком (вызывная панель у калитки, антенна или спутниковое ТВ).

					Проект: Дом 331 м²	М 1:75
	Лист	№ док.	Подпись	Дата		
Дизайнер	Кырлан А.С.			04.11.26	План слаботочных сетей · 1-й этаж	Стадия: П; Лист: 61; Листов: 168

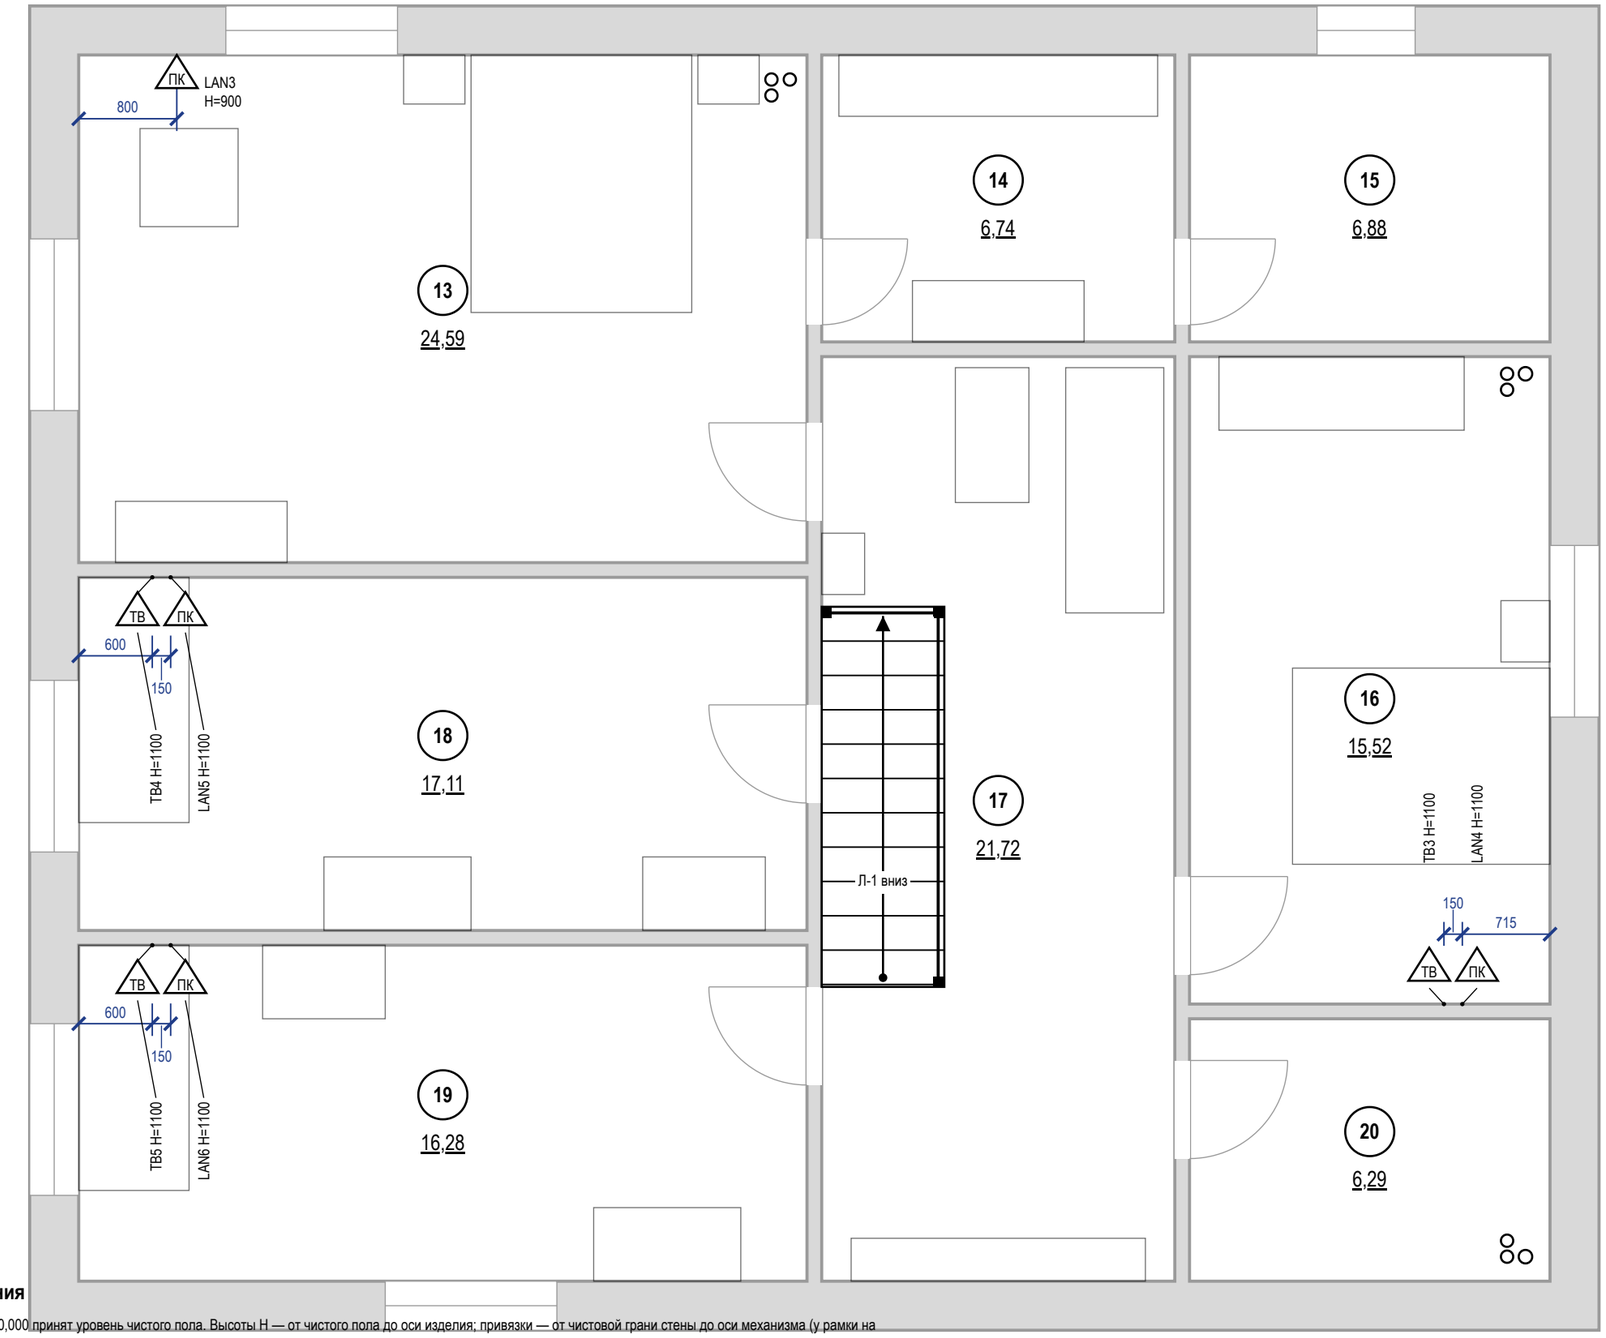

Ведомость слаботочных точек

Марка	Пом.	Назначение	H, мм	Кабель
LAN3	13	розетка LAN (RJ45)	900	U/UTP кат. 6
ТВ3	16	розетка ТВ	1100	RG-6
LAN4	16	розетка LAN (RJ45)	1100	U/UTP кат. 6
ТВ4	18	розетка ТВ	1100	RG-6
LAN5	18	розетка LAN (RJ45)	1100	U/UTP кат. 6
ТВ5	19	розетка ТВ	1100	RG-6
LAN6	19	розетка LAN (RJ45)	1100	U/UTP кат. 6


Условные обозначения

- ПК — розетка компьютерная RJ45
- ТВ — розетка телевизионная
- мебель и сантехприборы — подложка
- стояк: К1 — канализация, В1 — ХВС, Т3 — ГВС
- 1 — номер помещения, площадь м²

Примечания

1. За отметку 0,000 принят уровень чистого пола. Высоты H — от чистого пола до оси изделия; привязки — от чистовой грани стены до оси механизма (у рамки на несколько постов — до оси рамки).
2. Высота установки, не указанная на плане: розетки LAN и ТВ — 300 мм от чистого пола.
3. Слаботочные кабели — отдельно от силовых: в своей трубе или лотке, при параллельной прокладке не ближе 100 мм к силовым, пересечения под прямым углом; каждую точку — отдельным кабелем от ЩС без скруток.
4. Трассы на листе — принципиальные; фактические зафиксировать исполнительной схемой до закрытия отделкой. Силовые линии, УЗО 30 мА, ДСУП, кабель нг(А)-LS — по листам розеток и щита.
5. Проект силовой части и расчёт токов КЗ — по проекту ЭОМ; слаботочная часть согласуется с провайдером (ввод в дом, место ONT) и с заказчиком (вызывная панель у калитки, антенна или спутниковое ТВ).

					Проект: Дом 331 м²	М 1:50
	Лист	№ док.	Подпись	Дата	План слаботочных сетей · Мансарда	Стадия / Лист / Листов
Дизайнер	Кырлан А.С.			04.11.26		П / 62 / 168

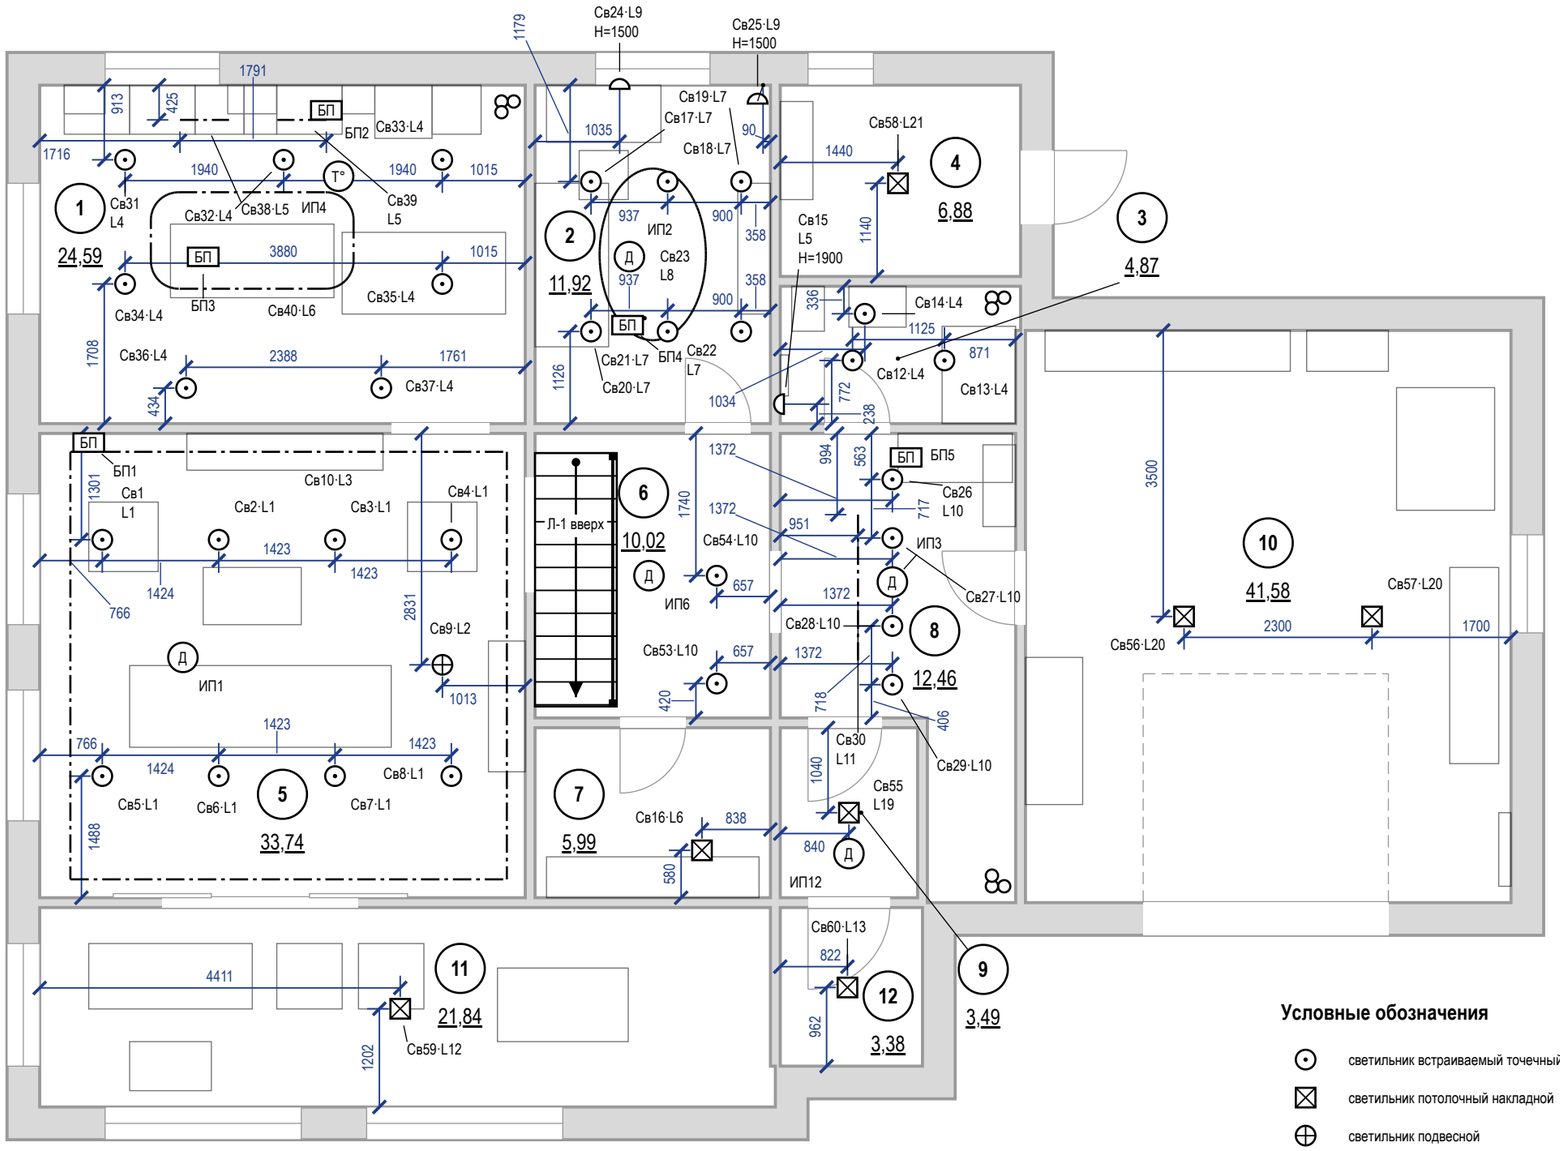

Условные обозначения

- светильник встраиваемый точечный
- светильник потолочный накладной
- светильник подвесной
- светильник настенный (бра), H высота оси
- светодиодная лента в профиле / в карнизе короба
- Св1·L1 — марка светильника (как в ведомости и на развёртках) · группа включения L (лист 67)
- Д — извещатель пожарный дымовой автономный
- Т° — извещатель пожарный тепловой
- БП — блок питания LED, с доступом (люк от 100×100 мм)
- мебель и сантехприборы — подложка
- стояк: К1 — канализация, В1 — ХВС, Т3 — ГВС
- 1 — номер помещения, площадь м²

Примечания

1. За отметку 0,000 принят уровень чистого пола. Высоты H — от чистого пола до оси изделия; привязки — от чистовой грани стены до оси механизма (у рамки на несколько постов — до оси рамки).
2. Высота установки, не указанная на плане: светильники — на потолке; настенные — по отметке H у знака. Привязки — до оси светильника от чистовой грани стены, по рядам.
3. Во влажных помещениях — светильники не ниже IP44; в зонах 0–2 ванной — по ГОСТ Р 50571.7.701-2024 (зона 1 — IPX5).
4. LED-лента в карнизе подсветки короба — по линии карниза с плана потолков; блок питания — в люке короба (БП на плане), питание ленты длиннее 5 м — с двух концов.
5. Розеточные и мокрые линии — через УЗО или дифавтомат с током утечки не более 30 мА (ПУЭ 7.1.79); в санузле выполнить ДСУП (ПУЭ 7.1.87–7.1.88).
6. Кабель — медный, исполнение нг(A)-LS (ГОСТ 31565-2012); скрытая прокладка только горизонтально и вертикально, фактические трассы зафиксировать исполнительной схемой до закрытия отделкой.
7. Расчёт нагрузок, токов КЗ, селективности и сечений — по проекту ЭОМ организации с допуском СРО; лист задаёт состав, расположение и группы.
8. Ведомость светильников (тип, количество, мощность, поток, Tц, Ra) — лист 65.


	Лист	№ док.	Подпись	Дата
Дизайнер	Кырлан А.С.			04.11.26

Проект: Дом 331 м² — **М 1:75**

План освещения · 1-й этаж

Стадия	Лист	Листов
П	63	168

выпуск 04.11.2026 № f163a372b2 · стр. 63 из 168

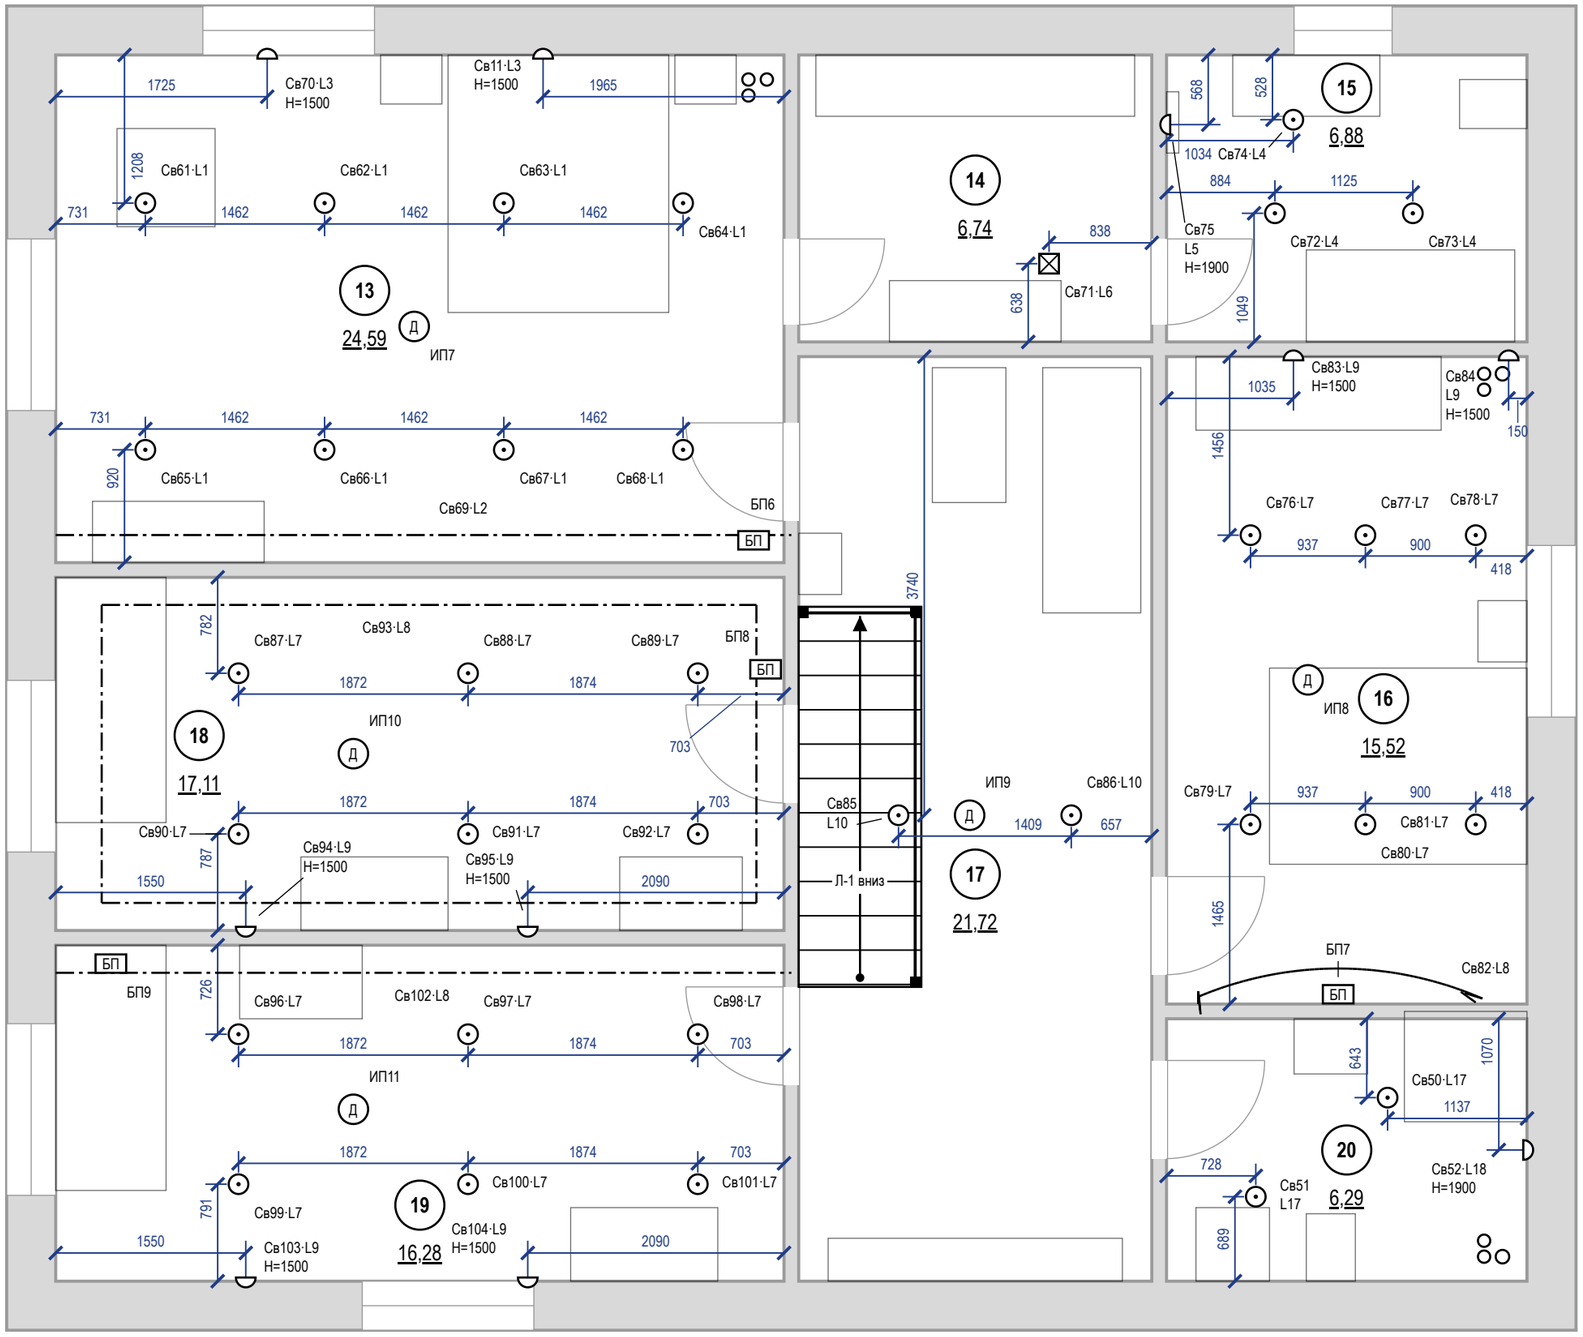

Условные обозначения

- светильник встраиваемый точечный
- светильник потолочный накладной
- светильник настенный (бра), H — высота оси
- светодиодная лента в профиле / в карнизе короба
- Св1·L1 — марка светильника (как в ведомости и на развёртках) · группа включения L (лист 67)
- Д — извещатель пожарный дымовой автономный
- БП — блок питания LED, с доступом (люк от 100×100 мм)
- мебель и сантехприборы — подложка
- стояк: К1 — канализация, В1 — ХВС, Т3 — ГВС
- 1 — номер помещения, площадь м²

Примечания

1. За отметку 0,000 принят уровень чистого пола. Высоты H — от чистого пола до оси изделия; привязки — от чистовой грани стены до оси механизма (у рамки на несколько постов — до оси рамки).
2. Высота установки, не указанная на плане: светильники — на потолке; настенные — по отметке H у знака. Привязки — до оси светильника от чистовой грани стены, по рядам.
3. Во влажных помещениях — светильники не ниже IP44; в зонах 0–2 ванной — по ГОСТ Р 50571.7.701-2024 (зона 1 — IPX5).
4. LED-лента в карнизе подсветки короба — по линии карниза с плана потолков; блок питания — в люке короба (БП на плане), питание ленты длиннее 5 м — с двух концов.
5. Розеточные и мокрые линии — через УЗО или дифавтомат с током утечки не более 30 мА (ПУЭ 7.1.79); в санузле выполнить ДСУП (ПУЭ 7.1.87–7.1.88).
6. Кабель — медный, исполнение нг(А)-LS (ГОСТ 31565-2012); скрытая прокладка только горизонтально и вертикально, фактические трассы зафиксировать исполнительной схемой до закрытия отделки.
7. Расчёт нагрузок, токов КЗ, селективности и сечений — по проекту ЭОМ организации с допуском СРО; лист задаёт состав, расположение и группы.
8. Ведомость светильников (тип, количество, мощность, поток, Tц, Ra) — лист 65.

					Проект: Дом 331 м²	M 1:50
	Лист	№ док.	Подпись	Дата		
Дизайнер	Кырлан А.С.			04.11.26	План освещения · Мансарда	Стадия: П; Лист: 64; Листов: 168

выпуск 04.11.2026 № f163a372b2 · стр. 64 из 168

Параметры светильников для подбора

Поз.	Марки	Наименование	Установка	Кол.	P, Вт	Σ P, Вт	Ф, лм	Тц, К	Ra	Угол, °	IP	Дим.	Слой	Группа	Пом.
1	Св1–Св8, Св31–Св37	Встраиваемый точечный	в ГКЛ, корпус ≤ 70 мм	15	12	180	1000	3000	90	—	20	—	общий	L1, L4	1, 5
2	Св38, Св39	Линейный светильник	на поверхности	1,2 м	8	16	700	3000	90	—	20	—	рабочий	L5	1
3	Св40	Лента светодиодная 24 В	в нише уровня, профиль с рассеивателем	10,2 м	9,6/м	97,8	900/м	2700	90	—	20	да	акцентный	L6	1
4	Св17–Св22, Св76–Св81, Св87–Св92, Св96–Св101	Встраиваемый точечный	в ГКЛ, корпус ≤ 70 мм	24	12	288	1050	2700	90	—	20	—	общий	L7	2, 16, 18, 19
5	Св23	Лента светодиодная 24 В	в нише уровня, профиль с рассеивателем	5,4 м	9,6/м	51,9	900/м	2700	90	—	20	да	акцентный	L8	2
6	Св11, Св24, Св25, Св70, Св83, Св84, Св94, Св95, Св103, Св104	Настенный (бра)	на стене, H=1500	10	6	60	400	2700	90	60	20	да	рабочий	L3, L9	2, 13, 16, 18, 19
7	Св12–Св14, Св51, Св72–Св74	Встраиваемый точечный	в ГКЛ, корпус ≤ 70 мм	7	6	42	500	3000	90	—	44	—	общий	L4, L17	3, 15, 20
8	Св15, Св52, Св75	Настенный светильник над зеркалом, драйвер встроен	над зеркалом, H=1900	3	8	24	600	3000	90	—	44	—	рабочий	L5, L18	3, 15, 20
9	Св16, Св55, Св58, Св71	Потолочный накладной	на потолке	4	10	40	900	3000	90	—	20	—	общий	L6, L19, L21	4, 7, 9, 14
10	Св9	Подвесной	подвес, низ H=1600	1	15	15	1200	2700	90	—	20	—	рабочий	L2	5
11	Св10	Лента светодиодная 24 В	в карнизе короба, профиль с рассеивателем	21,1 м	9,6/м	202,9	900/м	2700	90	—	20	да	акцентный	L3	5
12	Св26–Св29, Св53, Св54, Св85, Св86	Встраиваемый точечный	в ГКЛ, корпус ≤ 70 мм	8	7	56	600	3000	90	—	20	—	общий	L10	6, 8, 17
13	Св30	Лента светодиодная 24 В	на поверхности, профиль с рассеивателем, датчик движения	1,8 м	4,8/м	8,6	150/м	2700	90	—	20	нет	ночной	L11	8
14	Св56, Св57	Потолочный накладной	на потолке	2	24	48	2500	3000	90	—	20	—	общий	L20	10
15	Св59, Св60	Накладной точечный светильник (downlight)	на потолке	2	9	18	800	3000	90	—	44	—	общий	L12, L13	11, 12
16	Св61–Св68	Встраиваемый точечный	в ГКЛ, корпус ≤ 70 мм	8	12	96	1000	2700	90	—	20	—	общий	L1	13
17	Св69, Св102	Лента светодиодная 24 В	в карнизе короба, профиль с рассеивателем	12 м	9,6/м	115,2	900/м	2700	90	—	20	да	акцентный	L2, L8	13, 19
18	Св82	Лента светодиодная 24 В	в нише уровня, профиль с рассеивателем	3,2 м	9,6/м	30,4	900/м	2700	90	—	20	да	акцентный	L8	16
19	Св93	Лента светодиодная 24 В	в карнизе короба, профиль с рассеивателем	15,5 м	9,6/м	149,2	900/м	2700	90	—	20	да	акцентный	L8	18
20	Св50	Встраиваемый точечный	в ГКЛ, корпус ≤ 70 мм	1	7	7	600	3000	90	—	44	—	общий	L17	20
		Итого		**85 шт + 70,4 м**		**1546,2**									

LED-ленты, линейные светильники и блоки питания

Марка	Пом.	L, м	U, В	Вт/м	Σ P, Вт	БП	P БП, Вт	Загр., %	Питание	Доступ к БП
Св38	1	0,6	24	—	8	БП2	30	53	встроенный ввод	в навесном модуле M_10, съёмная панель
Св39	1	0,6	24	—	8	БП2	30	53	встроенный ввод	в навесном модуле M_10, съёмная панель
Св40	1	10,2	24	9,6	97,8	БП3	150	65	с двух концов	люк 300×300 в нише фигуры потолка ПТ1
Св23	2	5,4	24	9,6	51,9	БП4	200	26	с двух концов	люк 300×300 в нише фигуры потолка ПТ2
Св10	5	21,1	24	9,6	202,9	БП1	300	68	с двух концов	люк 300×300 в коробе потолка ПТ2
Св30	8	1,8	24	4,8	8,6	БП5	20	43	с одного конца	в шкафу M_24, верхняя полка
Св69	13	6	24	9,6	57,6	БП6	200	29	с двух концов	люк 300×300 в коробе потолка ПТ5
Св82	16	3,2	24	9,6	30,4	БП7	200	15	с двух концов	люк 300×300 в нише фигуры потолка ПТ5
Св93	18	15,5	24	9,6	149,2	БП8	200	75	с двух концов	люк 300×300 в коробе потолка ПТ5
Св102	19	6	24	9,6	57,6	БП9	200	29	с двух концов	люк 300×300 в коробе потолка ПТ5

Сценарии (помещения со светорегуляторами)

Помещение	Сценарий	Горят группы (уровень)	Управление
5. Гостиная	Вечер	L2 подвес над обеденным столом — вкл.; L3 лента в карнизе (диммер) — 50 %; остальные выкл.	светорегулятор S2; выключатель S1
	Гости	L1 общий свет (споты) — вкл.; L2 подвес над обеденным столом — вкл.; L3 лента в карнизе (диммер) — 100 %	светорегулятор S2; выключатель S1
	Кино	L3 лента в карнизе (диммер) — 20 %; остальные выкл.	светорегулятор S2
	Уборка	L1 общий свет (споты) — вкл.; L2 подвес над обеденным столом — вкл.; остальные выкл.	выключатель S1
13. Спальня мастер	Вечер	L2 подсветка короба — вкл.; L3 бра — 100 %; остальные выкл.	выключатели S3, S21, S22
	Уборка	L1 споты — вкл.; L2 подсветка короба — вкл.; остальные выкл.	выключатели S3, S21, S22

Примечания

1. Позиции и марки Св — те же, что на плане освещения (листы 63, 64); группы L — по плану выключателей (листы 67, 68).
2. Модели светильников не выбраны: лист — техническое задание на подбор. Модель по строке таблицы: поток, Тц, Ra, угол, IP и регулировка яркости не хуже указанных, мощность не больше; встраиваемые — под глубину короба (графа «Установка»). IP 20 — сухие помещения. После выбора моделей (артикул, производитель) лист выпускается как «Спецификация светильников».
3. Длина LED-ленты в карнизе и нише уровня — по линиям карниза и ниши плана потолков (листы 48, 49); Σ P = Вт/м × длина. Блок питания загружен не больше чем на 80 %; лента 24 В длиннее 10 м питается с двух концов; доступ к блоку питания — люк ревизии 300×300 мм или место, указанное в таблице.
4. Сценарии: % — яркость группы на светорегуляторе; «вкл.» — группа на обычной клавише; группы, не названные в строке, выключены. Светильники и блоки питания групп на светорегуляторе — с регулировкой яркости. Клавиши и светорегуляторы — листы 67, 68.
5. В пом. 2, 16, 18, 19 свет включается клавишами групп — листы 67, 68.
6. Мощность и поток в таблице — требования к подбору (поток не меньше, мощность не больше указанных); после выбора модели — по её паспорту, Σ P — установленная мощность освещения. Оценка освещённости — на плане освещения; это не светотехнический расчёт.

					Проект: Дом 331 м²
	Лист	№ док.	Подпись	Дата	
Дизайнер	Кырлан А.С.			04.11.26	Техническое задание на подбор светильников

Стадия	Лист	Листов
П	65	168

Слои света по помещениям

Пом.	Помещение	Слои света — группы включения (марки — в спецификации)	Σ P, Вт
1	Кухня-столовая	общий — L4; рабочий — L5; акцентный — L6	197,8
2	Кабинет-гостевая	общий — L7; рабочий — L9; акцентный — L8	135,9
3	Санузел 1 этажа	общий — L4; рабочий — L5	26
4	Котельная	общий — L21	10
5	Гостиная	общий — L1; рабочий — L2; акцентный — L3	313,9
6	Холл с лестницей	общий — L10	14
7	Кладовая	общий — L6	10
8	Прихожая	общий — L10; ночной — L11	36,6
9	Тамбур	общий — L19	10
10	Гараж	общий — L20	48
11	Веранда	общий — L12	9
12	Крыльцо	общий — L13	9
13	Спальня мастер	общий — L1; рабочий — L3; акцентный — L2	165,6
14	Гардеробная мастер	общий — L6	10
15	Санузел мастер	общий — L4; рабочий — L5	26
16	Спальня 2	общий — L7; рабочий — L9; акцентный — L8	114,4
17	Холл мансарды	общий — L10	14
18	Спальня 3	общий — L7; рабочий — L9; акцентный — L8	233,2
19	Спальня 4	общий — L7; рабочий — L9; акцентный — L8	141,6
20	Санузел 2	общий — L17; рабочий — L18	21

Слои света

общий — равномерный свет помещения, по норме освещённости

рабочий — местный свет задачи: столешница, зеркало, чтение у кровати

акцентный — подсветка потолка, стен и ниш; не входит в поток общего света


ночной — путь спальня → санузел: не выше 2700 K, малая яркость, датчик движения

Примечания

1. Продолжение листа 65: позиции, марки и группы — те же, что на основном листе.
2. Σ P — установленная мощность освещения помещения, Вт; группы L — по плану выключателей.

					Проект: Дом 331 м²
	Лист	№ док.	Подпись	Дата	Техническое задание на подбор светильников (продолжение)
Дизайнер	Кырлан А.С.			04.11.26	

Стадия	Лист	Листов
П	66	168

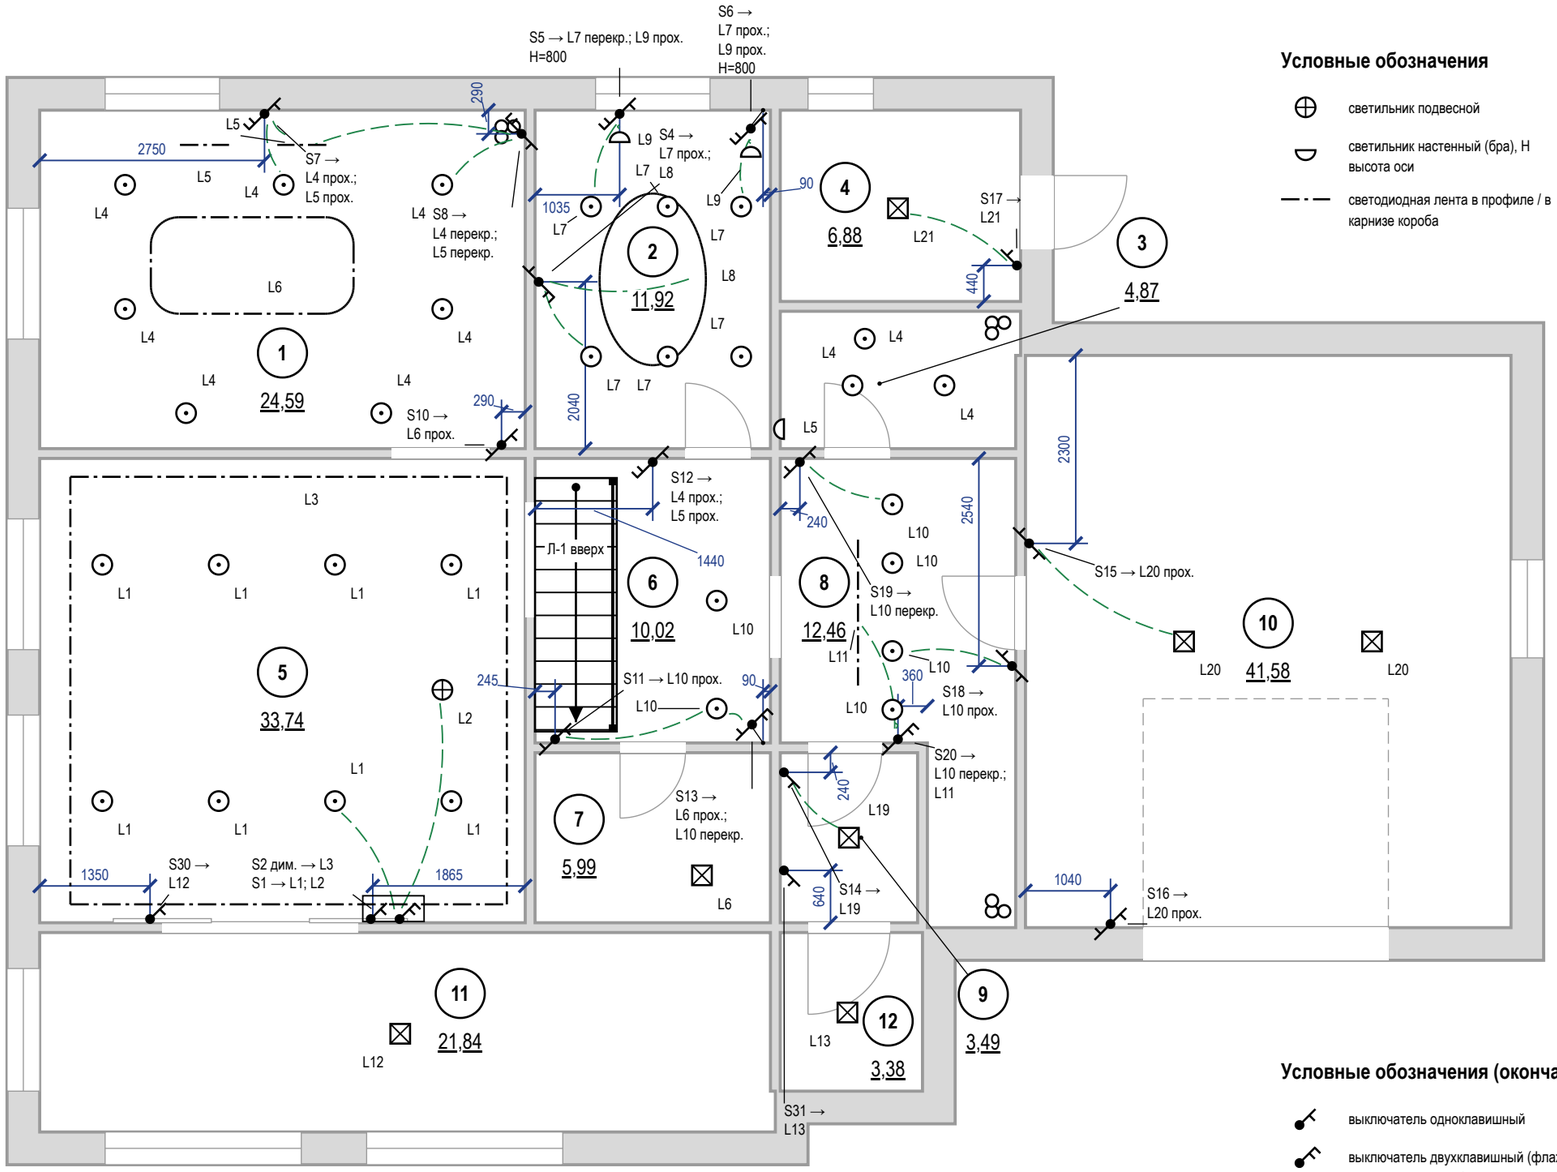

Условные обозначения

- светильник подвесной
- светильник настенный (бра), H высота оси
- светодиодная лента в профиле / в карнизе короба
- L1 — группа включения у светильника
- стояк: К1 — канализация, В1 — ХВС, Т3 — ГВС
- 1 — номер помещения, площадь м²


Примечания

1. За отметку 0,000 принят уровень чистого пола. Высоты H — от чистого пола до оси изделия; привязки — от чистовой грани стены до оси механизма (у рамки на несколько постов — до оси рамки).
2. Высота установки, не указанная на плане: выключатели — 900 мм от чистого пола (у кровати и другие — H у марки), со стороны дверной ручки (ПУЭ 7.1.51).
3. Какой выключатель какие светильники включает — по номеру группы L: у выключателя (S1 → L1; L2 — клавиши по порядку) и у каждого светильника. Пунктир — подсказка к ближайшему светильнику группы в том же помещении (не дальше 3 м), это не трасса кабеля; выключатель за стеной (у двери санузла) и далёкая группа — только номер группы.
4. Группы из нескольких мест (L4 — S7, S8, S12; L5 — S7, S8, S12; L6 — S10, S13; L7 — S4, S5, S6; L9 — S5, S6; L10 — S11, S13, S18, S19, S20; L20 — S15, S16): на крайних местах проходные клавиши, на промежуточных перекрёстные; механизмы — в ведомости изделий.
5. Светорегулятор — по заднему фронту (для LED-драйверов), совместимость с драйверами проверить до закупки.
6. Вентиляторы санузлов (выводы ЭВ на плане розеток) включаются вместе с основным светом помещения, отключаются с задержкой — таймер выбега в вентиляторе.
7. Розеточные и мокрые линии — через УЗО или дифавтомат с током утечки не более 30 мА (ПУЭ 7.1.79); в санузле выполнить ДСУП (ПУЭ 7.1.87–7.1.88).
8. Кабель — медный, исполнение нг(А)-LS (ГОСТ 31565-2012); скрытая прокладка только горизонтально и вертикально, фактические трассы зафиксировать исполнительной схемой до закрытия отделкой.
9. Расчёт нагрузок, токов КЗ, селективности и сечений — по проекту ЭОМ организации с допуском СРО; лист задаёт состав, расположение и группы.

Условные обозначения (окончание)

- выключатель одноклавишный
- выключатель двухклавишный (флажков — по числу клавиш)
- выключатель с проходной или перекрёстной клавишей (обратный флажок); тип клавиши — в подписи
- S1 → — марка → группы по клавишам (через «;»): прох. — проходной, перекр. перекрёстный, дим. светорегулятор; H — высота
- связь: выключатель → ближайший светильник группы в том же помещении (не трасса кабеля); полный состав группы — по номеру L
- светильник встраиваемый точечный
- светильник потолочный накладной

					Проект: Дом 331 м²	М 1:75
	Лист	№ док.	Подпись	Дата	Управление светильниками · 1-й этаж	Стадия: П; Лист: 67; Листов: 168
Дизайнер	Кырлан А.С.			04.11.26		

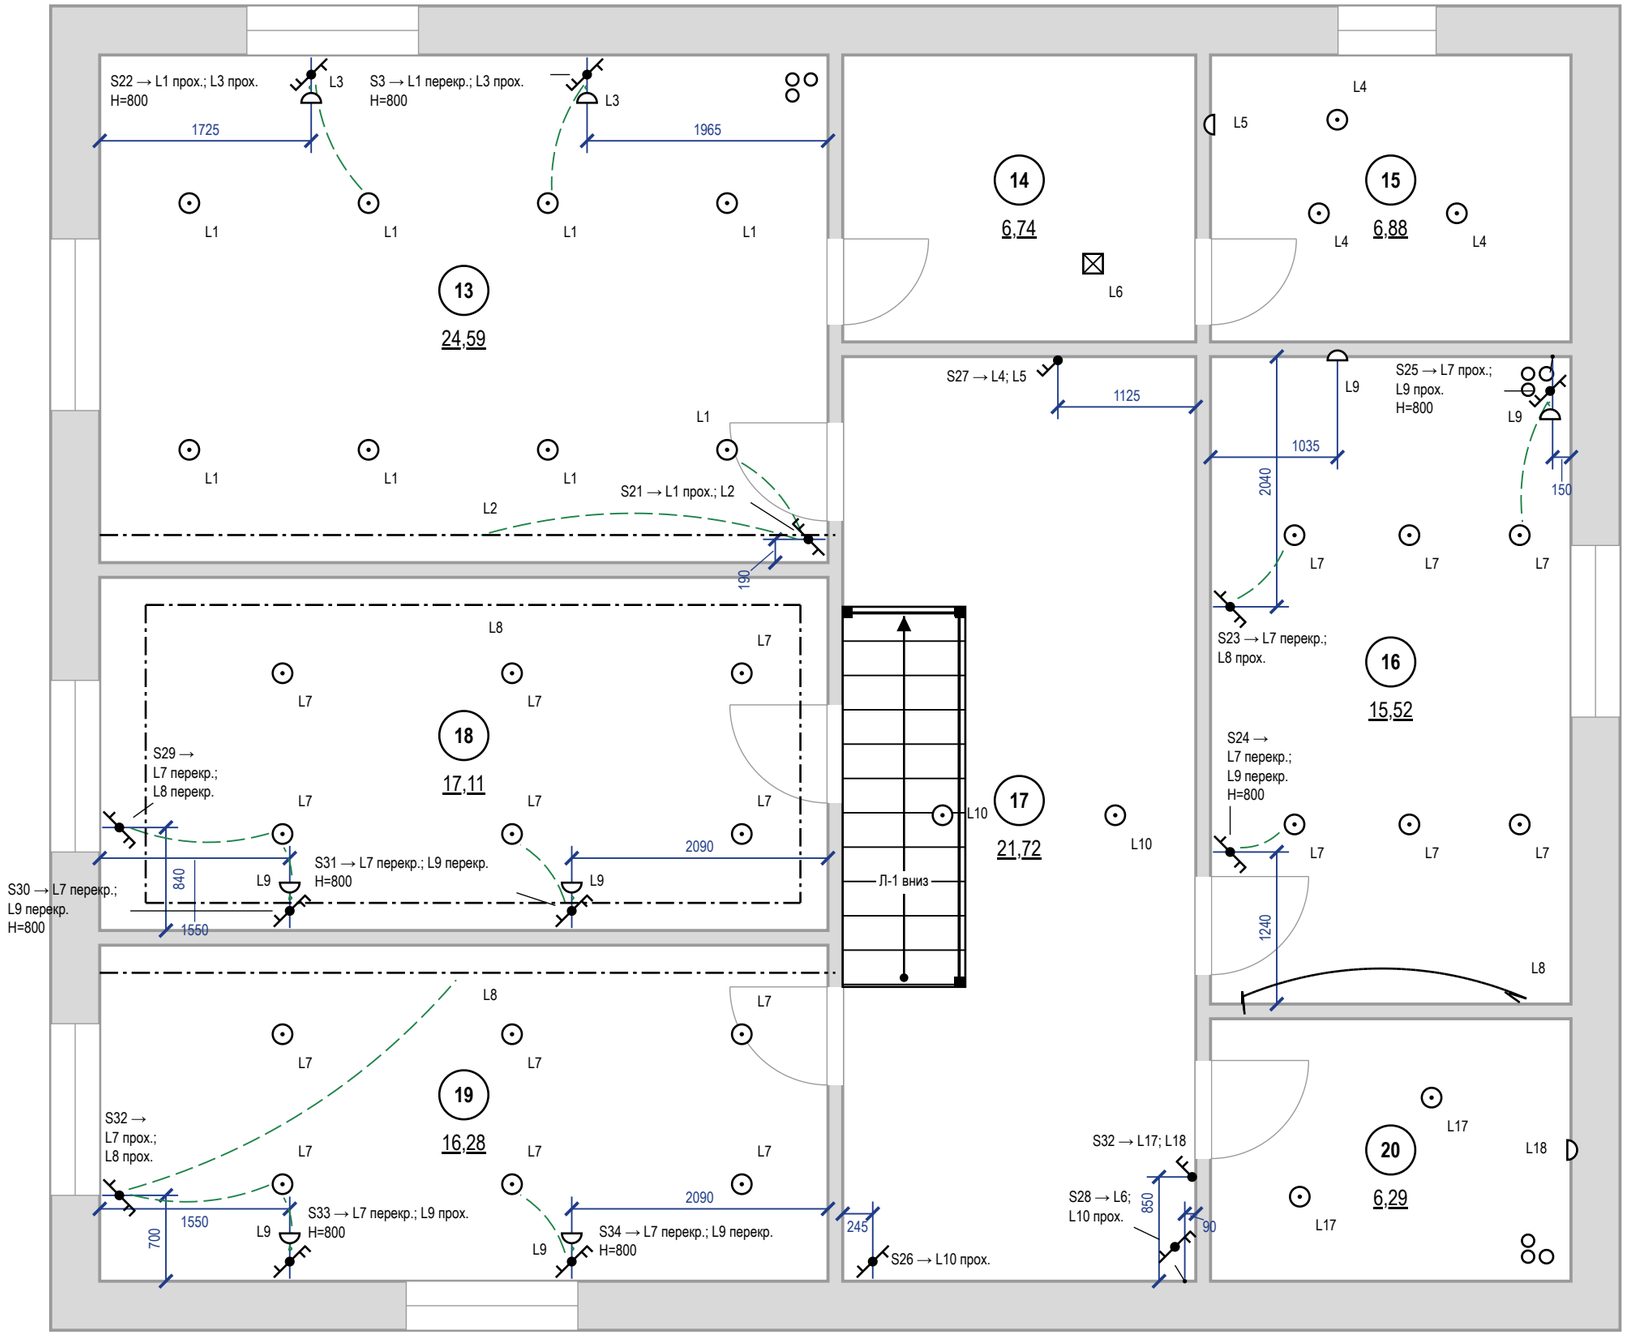


Условные обозначения

- выключатель двухклавишный (флажков — по числу клавиш)
- выключатель с проходной или перекрёстной клавишей (обратный флажок); тип клавиши — в подписи
- S1 → — марка → группы по клавишам (через «;»): прох. — проходной, перекр. — перекрёстный, дим. — светорегулятор; Н — высота
- связь: выключатель → ближайший светильник группы в том же помещении (не трасса кабеля); полный состав группы — по номеру L
- светильник встраиваемый точечный
- светильник потолочный накладной
- светильник настенный (бра), Н — высота оси
- светодиодная лента в профиле / в карнизе короба
- L1 — группа включения у светильника
- стояк: К1 — канализация, В1 — ХВС, Т3 — ГВС
- 1 — номер помещения, площадь м²

Примечания

1. За отметку 0,000 принят уровень чистого пола. Высоты Н — от чистого пола до оси изделия; привязки — от чистовой грани стены до оси механизма (у рамки на несколько постов — до оси рамки).
2. Высота установки, не указанная на плане: выключатели — 900 мм от чистого пола (у кровати и другие — Н у марки), со стороны дверной ручки (ПУЭ 7.1.51).
3. Какой выключатель какие светильники включает — по номеру группы L: у выключателя (S1 → L1; L2 — клавиши по порядку) и у каждого светильника. Пунктир — подсказка к ближайшему светильнику группы в том же помещении (не дальше 3 м), это не трасса кабеля; выключатель за стеной (у двери санузла) и далёкая группа только номер группы.
4. Группы из нескольких мест (L1 — S3, S21, S22; L3 — S3, S22; L7 S23, S24, S25, S29, S30, S31, S32, S33, S34; L8 — S23, S29, S32; L9 — S24, S25, S30, S31, S33, S34; L10 — S26, S28): на крайних местах — проходные клавиши, на промежуточных — перекрёстные; механизмы — в ведомости изделий.
5. Розеточные и мокрые линии — через УЗО или дифавтомат с током утечки не более 30 мА (ПУЭ 7.1.79); в санузле выполнить ДСУП (ПУЭ 7.1.87–7.1.88).
6. Кабель — медный, исполнение нг(А)-LS (ГОСТ 31565-2012); скрытая прокладка только горизонтально и вертикально, фактические трассы зафиксировать исполнительной схемой до закрытия отделкой.
7. Расчёт нагрузок, токов КЗ, селективности и сечений — по проекту ЭОМ организации с допуском СРО; лист задаёт состав, расположение и группы.

					Проект: Дом 331 м²	М 1:50
	Лист	№ док.	Подпись	Дата	Управление светильниками · Мансарда	Стадия / Лист / Листов
Дизайнер	Кырлан А.С.			04.11.26		П / 68 / 168

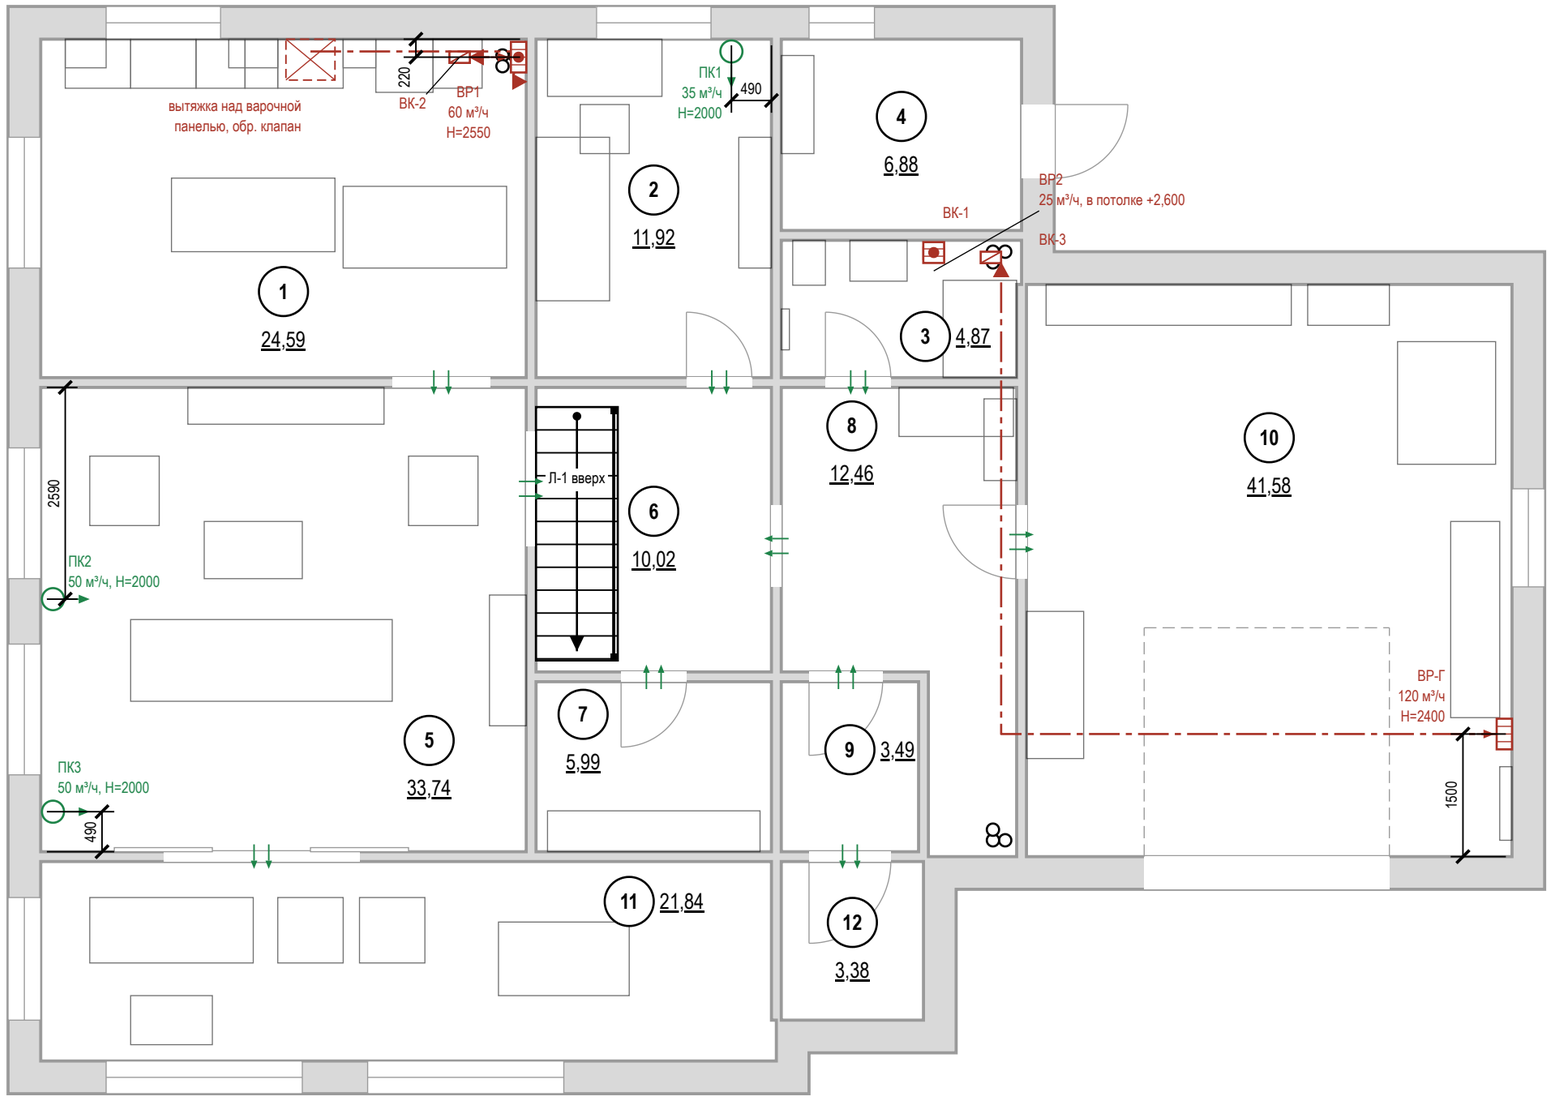

Условные обозначения

- стояк: К1 — канализация, В1 — ХВС, Т3 — ГВС
- номер помещения, площадь м²
- вытяжная решётка в вентканал: марка, расход м³/ч, Н центра от чистого пола
- вытяжная решётка с бытовым вентилятором и обратным клапаном: марка, расход, Н
- вентилятор с обратным клапаном в подшивном потолке, воздуховод за потолком до канала
- приточный клапан (КИВ) в наружной стене: марка, расход, Н центра
- переток: зазор под полотном или переточная решётка
- кухонная вытяжка над варочной панелью
- Вентканал ВК-N.
- воздуховод в коробе под потолком (за подшивным потолком) до вентканала
- отдельный вход воздуховода в вентканал, обратный клапан

Воздухообмен, м³/ч

№	Помещение	Выт. норма	Выт. проект	Прит. норма	Прит. проект	Устрой-ства
1	Кухня-столовая	60	60			ВР1
2	Кабинет-гостевая			34	35	ПК1
3	Санузел 1 этажа	25	25			ВР2
4	Котельная	4				наружу, см. прим.
5	Гостиная			95	100	ПК2, ПК3
7	Кладовая	3				переток
10	Гараж	23	120			ВР-Г
	Итого	**115**	**205**	**129**	**135**	

Воздухообмен этажа — по большей из сумм притока и вытяжки: норма 129 м³/ч, проект 205 м³/ч.
Вытяжка не меньше притока — баланс сведён.

Привязки — до обмера
Вентканалы ВК-N приняты проектировщиком, решётки и воздуховоды — от них. До черновых работ — обмер каналов и тяги, лист перевыпустить по факту.

Примечания


1. Расчёт систем ОВ и подбор оборудования — проектная организация с допуском СРО; лист даёт места, трассы и привязки.
2. Нормы одноквартирного дома — СП 55.13330.2016, п. 9.7: в жилых комнатах не менее однократного воздухообмена в час, из кухни не менее 60 м³/ч, из ванной, туалета, совмещённого санузла не менее 25 м³/ч; кухня с газовой плитой — 100 м³/ч в запас. Системы — по СП 60.13330.2020.
3. Вентканалы и шахты не сужать, не переносить и не закрывать; вентилятор и кухонная вытяжка — через обратный клапан, без перекрытия естественной тяги; ВР1 — воздуховодом до ВК-2 ≈ 0,7 м, ВР-Г — воздуховодом до ВК-3 ≈ 12,0 м (нужен вентилятор) в коробе под потолком.
4. Проектные расходы — не ниже нормы, вытяжка сведена с притоком вентиляторами мокрых помещений. Клапаны — в простенке у окна, центр 2000 мм, не над кроватью, не ближе 300 мм к стоякам отопления; типоразмер — на расход.
5. Под подшивным потолком вытяжка — в потолке, воздуховодом за потолком до канала. Кухонная вытяжка в воздухообмен не включена: воздуховод не менее Ø125 в коробе, вход в канал отдельный.
6. Переток — зазор под полотнами межкомнатных дверей или переточная решётка.
7. Котельная (пом. 4), Гараж (пом. 10) — вытяжка наружу своим каналом, воздух в жилую часть не перетекает (выхлоп, продукты сгорания); приток — с улицы. Воздухообмен котельной — по паспорту котла и СП 60.13330.2020, при газовом котле — СП 62.13330; тип котла не выбран — устройства не показаны до решения.
8. Кондиционирование заданием не предусмотрено; при установке трассы фреона и дренажа (не менее 40 мм/м, в К1 через сифон) и питание заложить до черновых работ.
9. Привязки оборудования — по паспортам приобретённых моделей, до черновых работ.

	Лист	№ док.	Подпись	Дата
Дизайнер	Кырлан А.С.			04.11.26

Проект: Дом 331 м² — **М 1:75**

План вентиляции · 1-й этаж

Стадия	Лист	Листов
П	69	168

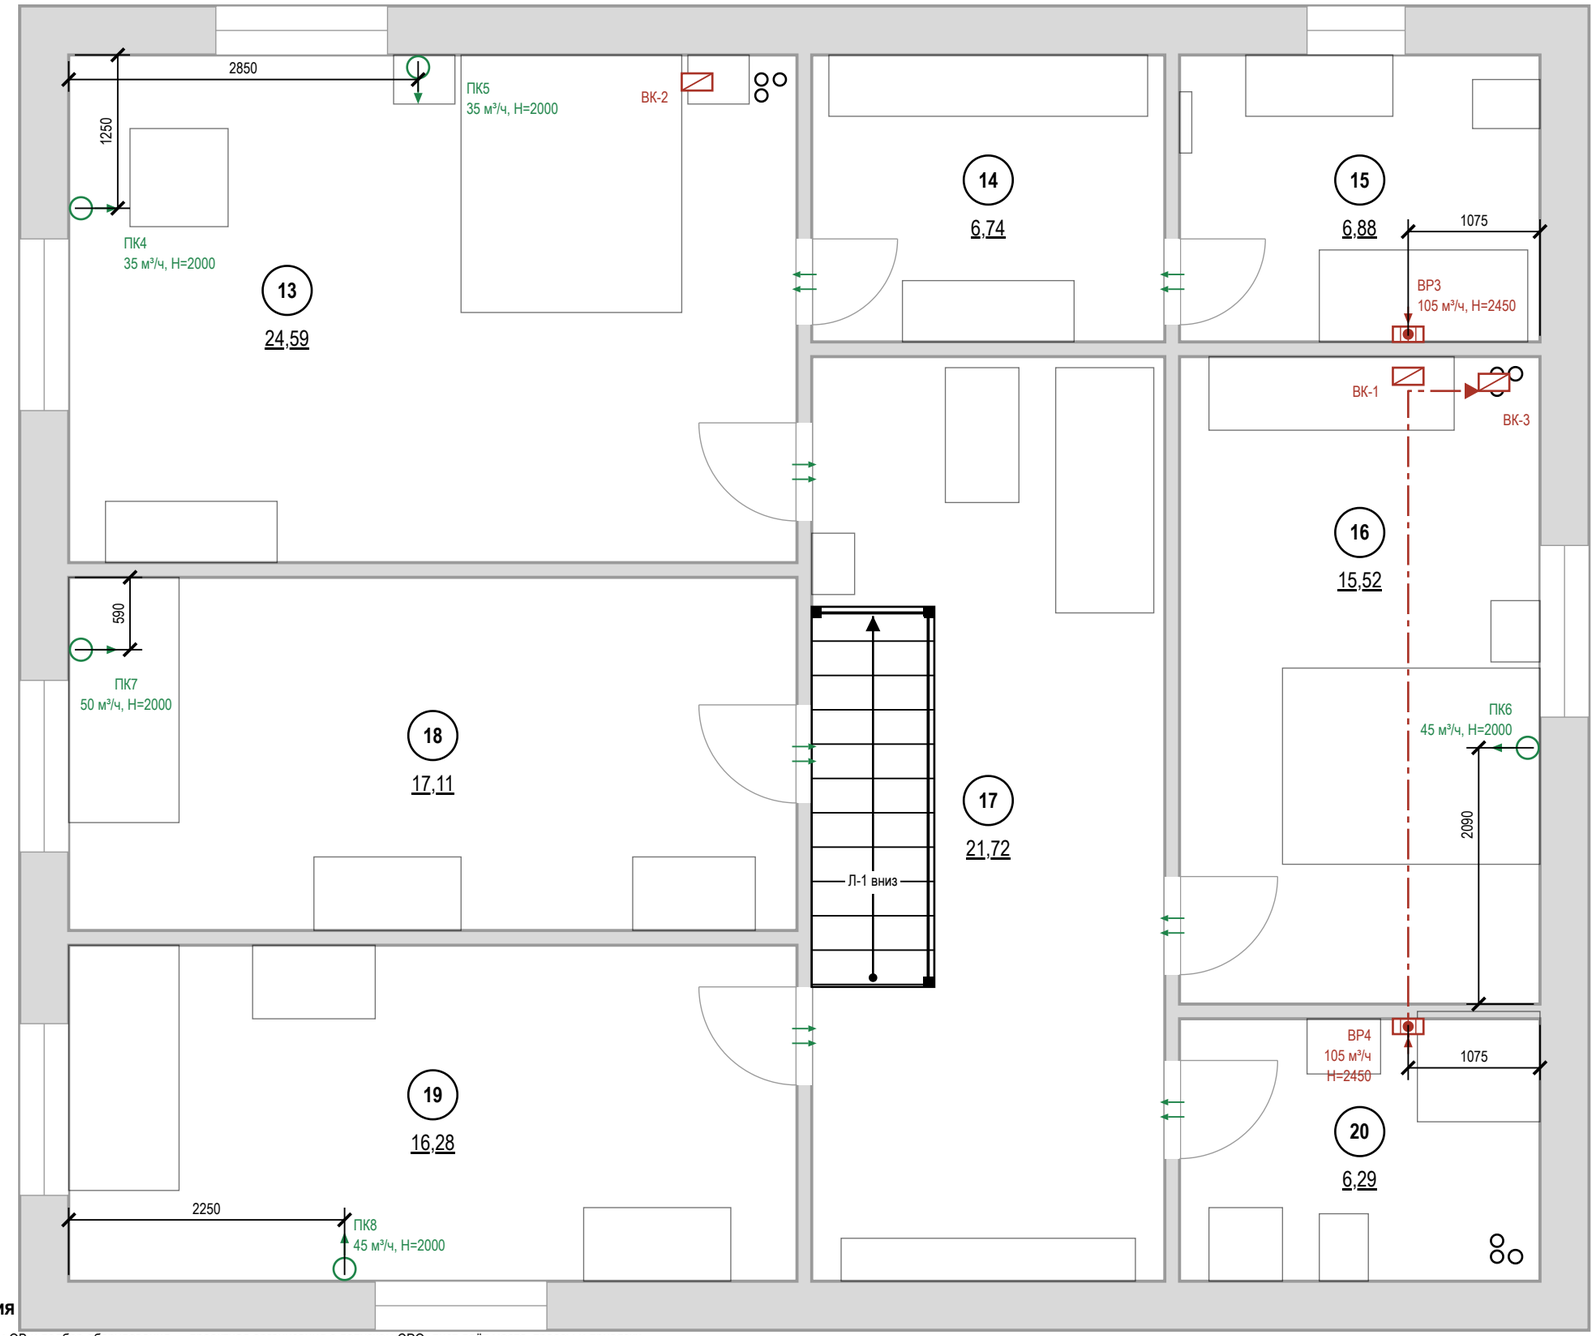

Условные обозначения

- стояк: К1 — канализация, В1 — ХВС, Т3 — ГВС
- номер помещения, площадь м²
- вытяжная решётка с бытовым вентилятором и обратным клапаном: марка, расход, Н
- приточный клапан (КИВ) в наружной стене: марка, расход, Н центра
- переток: зазор под полотном или переточная решётка
- Вентканал ВК-N.
- воздуховод в коробе под потолком (за подшивным потолком) до вентканала
- отдельный вход воздуховода в вентканал, обратный клапан

Воздухообмен, м³/ч

№	Помещение	Выт. норма	Выт. проект	Прит. норма	Прит. проект	Устрой-ства
13	Спальня мастер			67	70	ПК4, ПК5
14	Гардеробная мастер	4				переток
15	Санузел мастер	25	105			ВР3
16	Спальня 2			42	45	ПК6
18	Спальня 3			47	50	ПК7
19	Спальня 4			44	45	ПК8
20	Санузел 2	25	105			ВР4
	Итого	**54**	**210**	**200**	**210**	

Воздухообмен этажа — по большей из сумм притока и вытяжки: норма 200 м³/ч, проект 210 м³/ч.
Вытяжка не меньше притока — баланс сведён.

Привязки — до обмера
Вентканалы ВК-N приняты проектировщиком, решётки и воздуховоды — от них. До черновых работ — обмер каналов и тяги, лист перевыпустить по факту.

Примечания


1. Расчёт систем ОВ и подбор оборудования — проектная организация с допуском СРО; лист даёт места, трассы и привязки.
2. Нормы одноквартирного дома — СП 55.13330.2016, п. 9.7: в жилых комнатах не менее однократного воздухообмена в час, из кухни не менее 60 м³/ч, из ванной, туалета, совмещённого санузла не менее 25 м³/ч; кухня с газовой плитой — 100 м³/ч в запас. Системы — по СП 60.13330.2020.
3. Вентканалы и шахты не сужать, не переносить и не закрывать; вентилятор и кухонная вытяжка — через обратный клапан, без перекрытия естественной тяги; ВР4 — воздуховодом до ВК-3 ≈ 6,0 м в коробе под потолком.
4. Проектные расходы — не ниже нормы, вытяжка сведена с притоком вентиляторами мокрых помещений. Клапаны — в простенке у окна, центр 2000 мм, не над кроватью, не ближе 300 мм к стоякам отопления; типоразмер — на расход.
5. Переток — зазор под полотнами межкомнатных дверей или переточная решётка.
6. Кондиционирование заданием не предусмотрено; при установке трассы фреона и дренажа (не менее 40 мм/м, в К1 через сифон) и питание заложить до черновых работ.
7. Привязки оборудования — по паспортам приобретённых моделей, до черновых работ.

	Лист	№ док.	Подпись	Дата	
Дизайнер	Кырлан А.С.			04.11.26	

Проект: Дом 331 м² — **М 1:50**

План вентиляции · Мансарда

Стадия	Лист	Листов
П	70	168

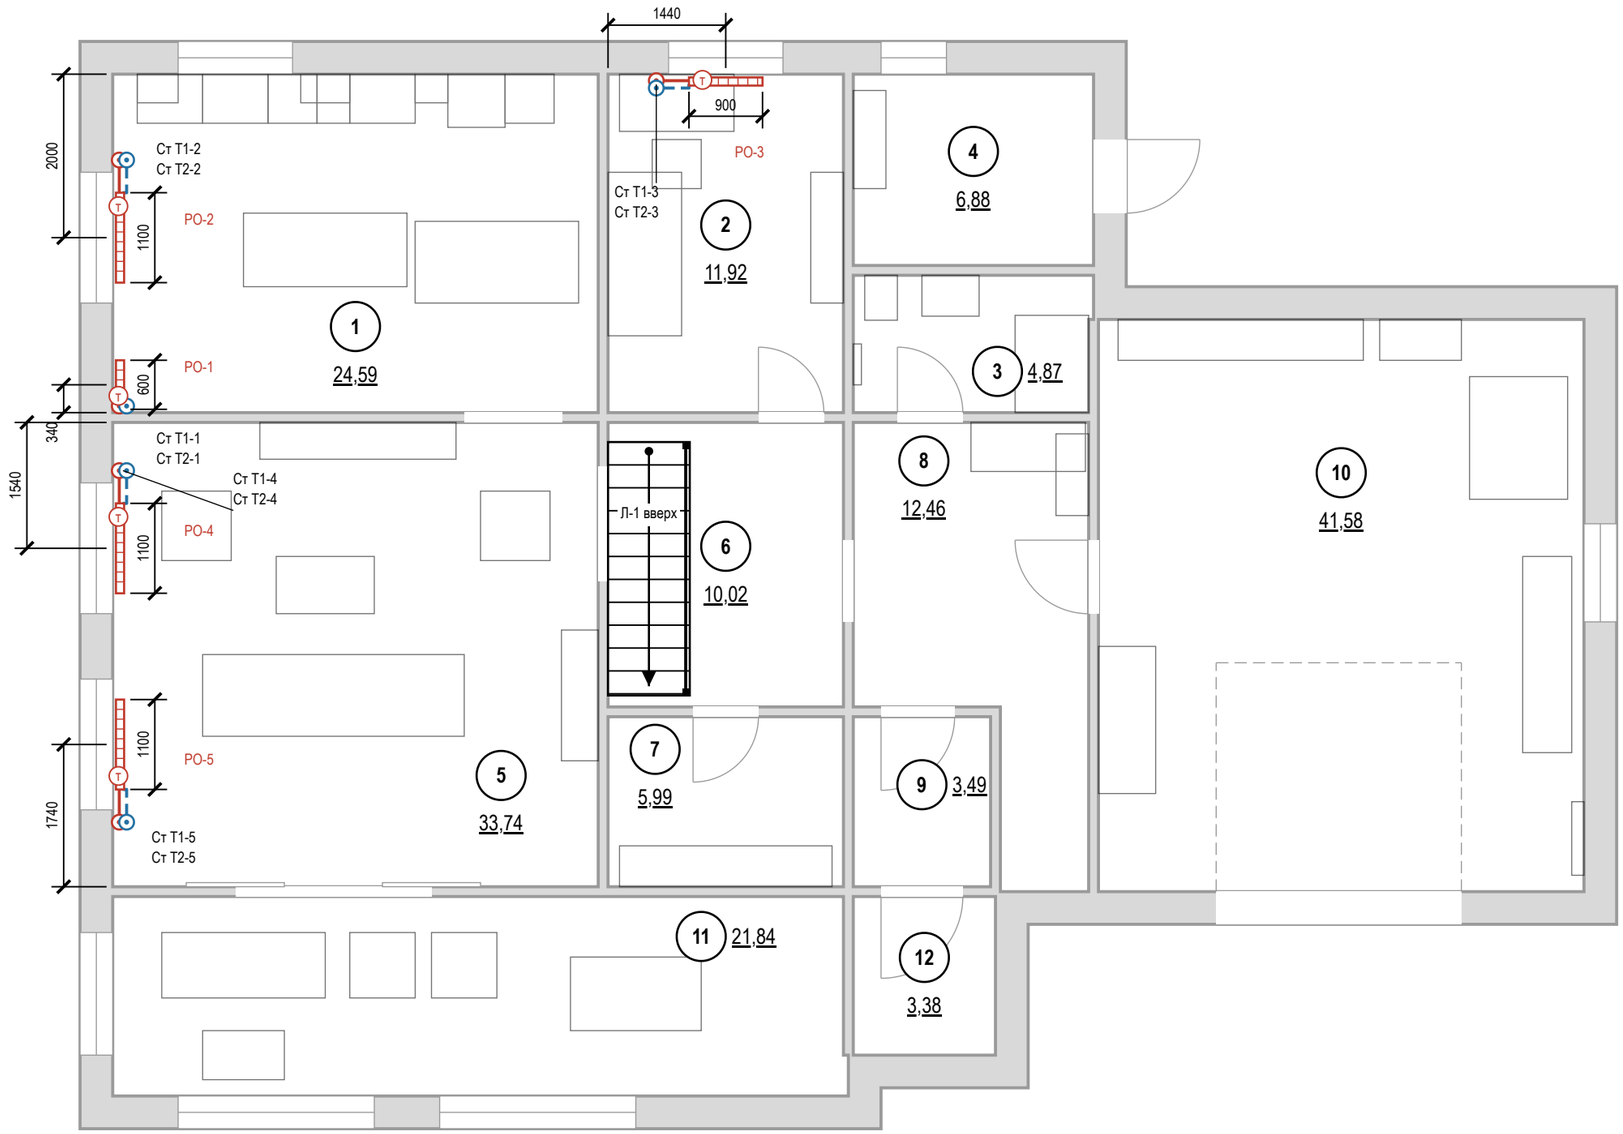

Условные обозначения

- (1) — номер помещения, площадь м²
- радиатор отопления (марка РО-N, длина по плану)
- (Т) — клапан с термоголовкой на подаче
- стояк отопления, подающий (Ст Т1-N)
- стояк отопления, обратный (Ст Т2-N)
- Т1 — отопление, подающий трубопровод
- Т2 — отопление, обратный трубопровод

Ведомость радиаторов

Марка	Помещение	Тип	Д×В×Г, мм	Низ / стена	Q, Вт
РО-1	1. Кухня-столовая		600×600×100	120 / 40	расч.
РО-2	1. Кухня-столовая		1100×600×100	120 / 40	расч.
РО-3	2. Кабинет-гостевая		900×600×100	120 / 40	расч.
РО-4	5. Гостиная		1100×600×100	120 / 40	расч.
РО-5	5. Гостиная		1100×600×100	120 / 40	расч.

Низ — от чистого пола, стена — зазор до задней панели, мм.

Привязки — до обмера


Подъёмы подводок отопления в исходных данных не заданы: показаны у откосов окон и у торцов приборов принципиально, разводка — от котла (котельная, пом. 4) через распределительный коллектор. До черновых работ — место котла, коллектора и подъёмов труб и паспорта приборов; лист перевыпустить по факту.

Примечания

1. Расчёт системы отопления, теплопотерь и подбор приборов — проектная организация с допуском СРО; лист даёт места и привязки.
2. Тип, длина и мощность радиаторов — по теплотехническому расчёту; лист задаёт места, зазоры и подключение.
3. Зазоры радиатора: низ не менее 100 мм от чистого пола, верх не менее 100 мм до подоконника, 30–50 мм от стены до задней панели; центр по оси окна с допуском ±20 мм. Верх до подоконника — 180 мм. Радиаторы не закрывать глухими коробами и мебелью; трубы через стены и перекрытия в гильзах.
4. Источник тепла — котёл в котельной (пом. 4): тип (газ / электро / твёрдое топливо) и мощность — по решению заказчика и расчёту (СП 60.13330.2020); до выбора разводка от коллектора принципиальная.
5. Без отопительного прибора: пом. 3, пом. 6, пом. 7 — внутренние, без наружных стен, окон и дверей наружу, обогреваются от смежных помещений; полотенцесушитель — по листам ВК.
6. Прибор не задан: пом. 8 (дверь наружу), 9 (дверь наружу) — прибор (у входной двери — конвектор) или тёплый пол по расчёту до черновых работ.
7. Привязки приборов и подводок — по паспортам приобретённых радиаторов и клапанов, до черновых работ.
8. До закрытия отделкой трубопроводы отопления испытать гидростатическим давлением с оформлением акта (СП 73.13330.2016, 7.2–7.3).

					Проект: Дом 331 м² — М 1:75
	Лист	№ док.	Подпись	Дата	
Дизайнер	Кырлан А.С.			04.11.26	План отопления · 1-й этаж

Стадия	Лист	Листов
П	71	168

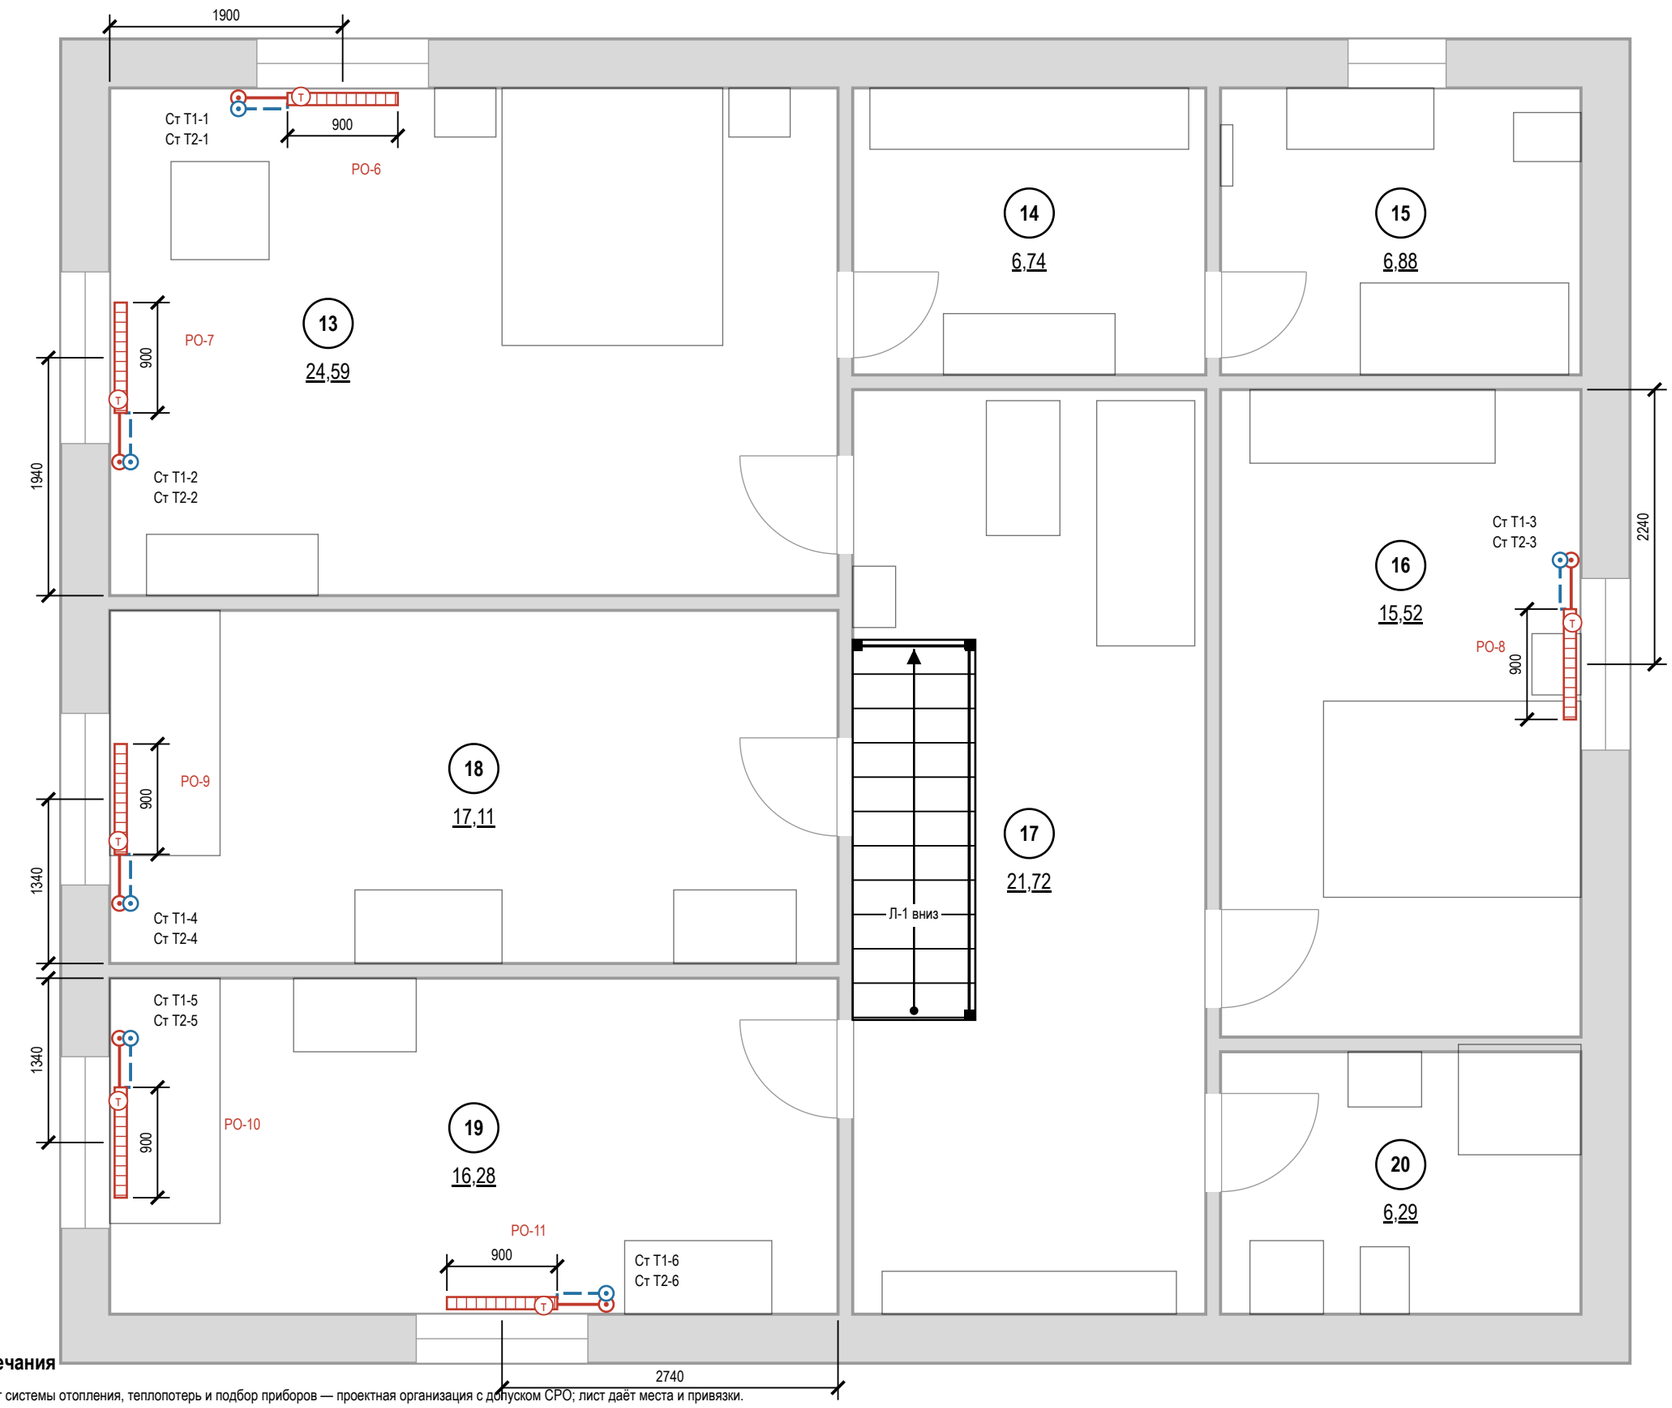

Условные обозначения

- (1) — номер помещения, площадь м²
- радиатор отопления (марка РО-N, длина по плану)
- клапан с термоголовкой на подаче
- стояк отопления, подающий (Ст Т1-N)
- стояк отопления, обратный (Ст Т2-N)
- Т1 — отопление, подающий трубопровод
- Т2 — отопление, обратный трубопровод

Ведомость радиаторов

Марка	Помещение	Тип	Д×В×Г, мм	Низ / стена	Q, Вт
РО-6	13. Спальня мастер		900×600×100	120 / 40	расч.
РО-7	13. Спальня мастер		900×600×100	120 / 40	расч.
РО-8	16. Спальня 2		900×600×100	120 / 40	расч.
РО-9	18. Спальня 3		900×600×100	120 / 40	расч.
РО-10	19. Спальня 4		900×600×100	120 / 40	расч.
РО-11	19. Спальня 4		900×600×100	120 / 40	расч.

Низ — от чистого пола, стена — зазор до задней панели, мм.


Привязки — до обмера

Подъёмы подводок отопления в исходных данных не заданы: показаны у откосов окон принципиально, разводка — от котла (котельная, пом. 4) через распределительный коллектор. До черновых работ — место котла, коллектора и подъёмов труб и паспорта приборов; лист перевыпустить по факту.

Примечания

1. Расчёт системы отопления, теплопотерь и подбор приборов — проектная организация с допуском СРО; лист даёт места и привязки.
2. Тип, длина и мощность радиаторов — по теплотехническому расчёту; лист задаёт места, зазоры и подключение.
3. Зазоры радиатора: низ не менее 100 мм от чистого пола, верх не менее 100 мм до подоконника, 30–50 мм от стены до задней панели; центр по оси окна с допуском ±20 мм. Верх до подоконника — 180 мм. Радиаторы не закрывать глухими коробами и мебелью; трубы через стены и перекрытия в гильзах.
4. Источник тепла — котёл в котельной (пом. 4): тип (газ / электро / твёрдое топливо) и мощность — по решению заказчика и расчёту (СП 60.13330.2020); до выбора разводка от коллектора принципиальная.
5. Прибор не задан: пом. 15, 17, 20 — прибор или тёплый пол по расчёту до черновых работ.
6. Привязки приборов и подводок — по паспортам приобретённых радиаторов и клапанов, до черновых работ.
7. До закрытия отделкой трубопроводы отопления испытать гидростатическим давлением с оформлением акта (СП 73.13330.2016, 7.2–7.3).

	Лист	№ док.	Подпись	Дата	
Дизайнер	Кырлан А.С.			04.11.26	Проект: Дом 331 м² — М 1:50
					План отопления · Мансарда — Стадия: П; Лист: 72; Листов: 168

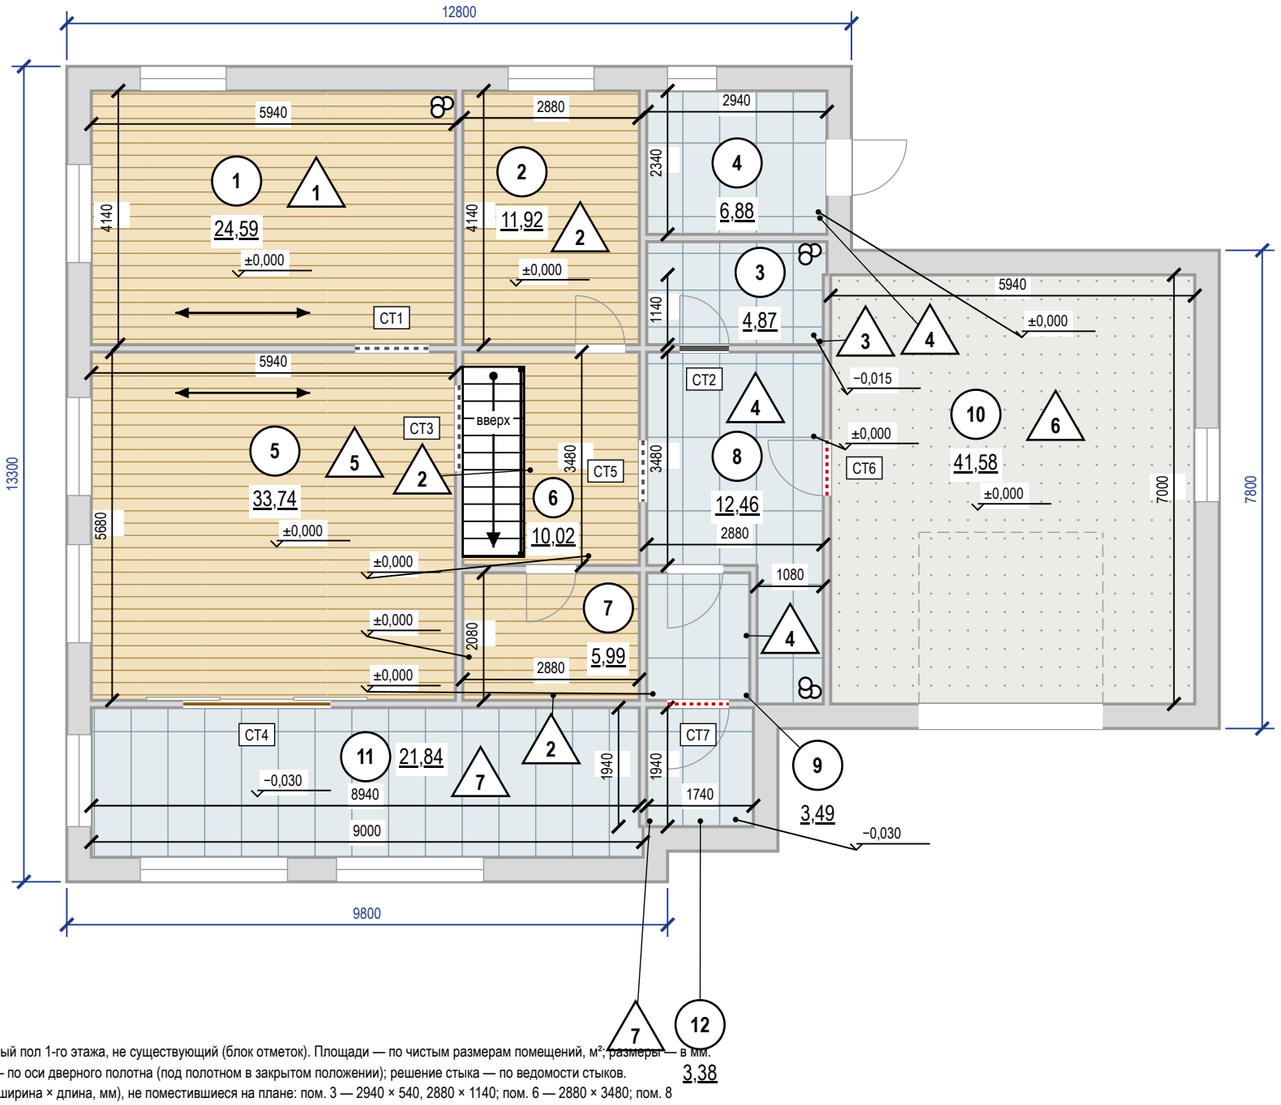

Экспликация полов

Номер помещения	Тип пола	Схема пола	Данные элементов пола (наименование, толщина, основание), мм	Площадь, м²
1	1		Инженерная доска дуб на клею — 14 Клей паркетный МС-полимерный — 1 Гидроизоляция полиуретановая, 2 слоя (зона мойки и острова) — 2 Стяжка ЦПС М300 (В22,5), фибра, по звукоизоляции — 47 Плита перекрытия монолитная Всего 64 мм; ЧП ±0,000, верх плиты −0,064	24,59
2, 6, 7	2		Инженерная доска на клею — 14 Стяжка ЦПС М200 — 50 Плита перекрытия Всего 64 мм; ЧП ±0,000, верх плиты −0,064	27,93
3	3		Керамогранит на клею С2 TE S1 — 14 Гидроизоляция обмазочная, 2 слоя, с заведением на стены 200 мм — 2 Стяжка ЦПС М200 — 33 Плита перекрытия Всего 49 мм; ЧП −0,015, верх плиты −0,064	4,87
4, 8, 9	4		Керамогранит на клею С2 TE S1 — 14 Стяжка ЦПС М200 — 50 Плита перекрытия Всего 64 мм; ЧП ±0,000, верх плиты −0,064	22,83
5	5		Инженерная доска дуб на клею — 14 Клей паркетный МС-полимерный — 1 Стяжка ЦПС М300 (В22,5), фибра, по звукоизоляции — 49 Плита перекрытия монолитная Всего 64 мм; ЧП ±0,000, верх плиты −0,064	33,74
10	6		Наливной полимерный пол с грунтом и кварцевой посыпкой — 3 Стяжка ЦПС М300, армированная сеткой — 61 Плита перекрытия по грунту Всего 64 мм; ЧП ±0,000, верх плиты −0,064	41,58
11, 12	7		Керамогранит 600×600×10 — 10 Клей плиточный С2 TE S1 (деформируемый) — 5 Сборное основание ГВЛВ 2×12,5 — 25 Пенополистирол экструзионный 2×50 100 Плита перекрытия монолитная Всего 140 мм; ЧП −0,030, верх плиты −0,170	25,22
			Итого	**180,76**


Отметки по высоте

±0,000	чистый пол пом. 1, 2, 4–10; отсчёт высот
−0,015	чистый пол пом. 3, ниже на 15 мм
−0,030	чистый пол пом. 11, 12, ниже на 30 мм
плита	верх плиты разный: −0,064, −0,170 (задание на обмер)
сущ. пол	снимается до плиты; не замерен (задание на обмер)



Примечания

1. За отметку ±0,000 принят чистый пол 1-го этажа, не существующий (блок отметок). Площади — по чистым размерам помещений, м²; размеры — в мм.
2. Стык разнотипных покрытий — по оси дверного полотна (под полотном в закрытом положении); решение стыка — по ведомости стыков.
3. Размеры помещений в свету (ширина × длина, мм), не поместившиеся на плане: пом. 3 — 2940 × 540, 2880 × 1140; пом. 6 — 2880 × 3480; пом. 8 2880 × 3480, 1080 × 2260; пом. 9 — 1680 × 2080.
4. Пол санузлов ниже смежных помещений на 15 мм; гидроизоляция по стяжке с заведением на стены не менее 200 мм (СП 29.13330.2011, п. 7.2), до облицовки — тест проливом и акт скрытых работ.
5. Трубопроводы в конструкции пола не прокладываются: пирог пола 49–140 мм не вмещает выпуски канализации с уклоном — выпуски К1 ведутся по стенам над чистым полом в коробах.
6. Штучные покрытия (инженерная доска): направление — по стрелке; влажность основания по СМ не более 2,0 % (по ТУ изготовителя).
7. Ровность основания — просвет под 2-метровой рейкой не более 2 мм: пом. 1, 2, 5, 6, 7 (инженерная доска), пом. 3, 4, 8, 9 (керамогранит), пом. 10 (наливной пол); 3 мм: пом. 11, 12 (керамогранит); проверить до укладки покрытия (СП 71.13330.2017, табл. 8.5).
8. Сетка на плитке — условная, в размер формата; точка старта и раскладка — по листу раскладки плитки.
9. Узор покрытия (заливка-код типа пола) прерывается под надписями — площадями помещений и отметками чистого пола.
10. Пироги полов — по экспликации полов: слои сверху вниз, толщины в мм; гидроизоляция мокрых зон — в пироге и в ведомости отделки; схема пола — без масштаба.

					Проект: Дом 331 м²	**М 1:100**
	Лист	№ док.	Подпись	Дата		
Дизайнер	Кырлан А.С.			04.11.26	План покрытий пола · 1-й этаж	Стадия: П; Лист: 73; Листов: 168

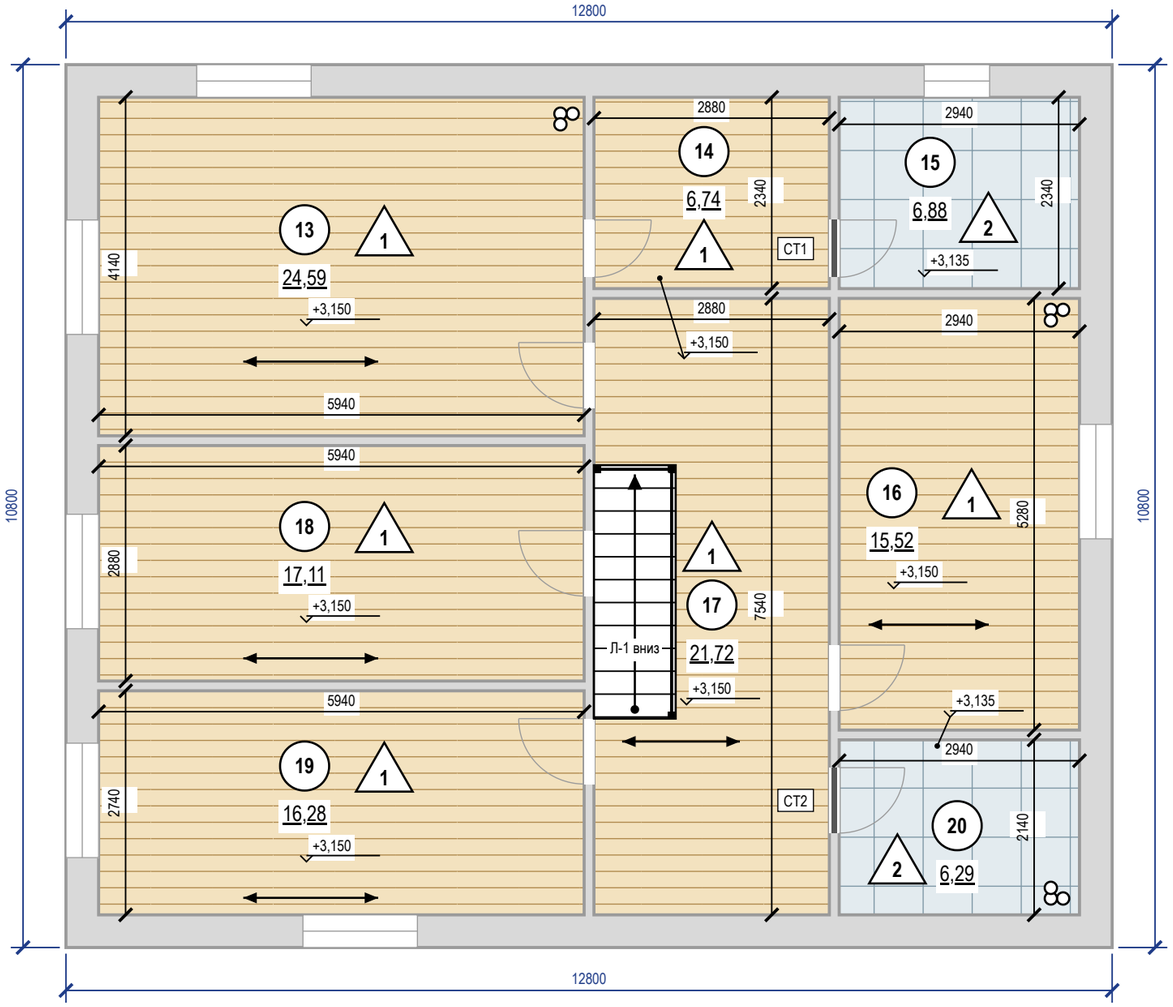

Экспликация полов

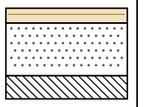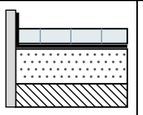Номер помещения	Тип пола	Схема пола	Данные элементов пола (наименование, толщина, основание), мм	Площадь, м²
13, 14, 16, 17, 18, 19	1		Инженерная доска на клею — 14 Стяжка ЦПС М200 — 50 Плита перекрытия Всего 64 мм; ЧП +3,150, верх плиты +3,086	101,96
15, 20	2		Керамогранит на клею C2 TE S1 — 14 Гидроизоляция обмазочная, 2 слоя, с заведением на стены 200 мм — 2 Стяжка ЦПС М200 — 33 Плита перекрытия Всего 49 мм; ЧП +3,135, верх плиты +3,086	13,17
			Итого	**115,13**

Раскладка покрытий

Пом.	Укладка	Старт (оси от чистовых стен), мм	Отступ 1-го ряда / крайние плитки, мм
13	вдоль стен A/B, прямая	от стены А, 1-й ряд вдоль неё	зазор от стены не задан
14	вдоль стен A/B, прямая	от стены А, 1-й ряд вдоль неё	зазор от стены не задан
15	прямая, сетка 600×600, шов 2	ось X 1446 от Г; ось Y 1146 от А	X 542 / 542; Y 543 / 543
16	вдоль стен A/B, прямая	от стены А, 1-й ряд вдоль неё	зазор от стены не задан
17	вдоль стен A/B, прямая	от стены А, 1-й ряд вдоль неё	зазор от стены не задан
18	вдоль стен A/B, прямая	от стены А, 1-й ряд вдоль неё	зазор от стены не задан
19	вдоль стен A/B, прямая	от стены В, 1-й ряд вдоль неё	зазор от стены не задан
20	прямая, сетка 600×600, шов 2	ось X 1446 от Г; ось Y 1046 от А	X 542 / 542; Y 443 / 443

Спецификация плинтусов

Наименование	Помещения	Длина, м (с запасом)
Плинтус МДФ под покраску 80×16, крепление к стене, окраска в цвет Farrow & Ball No. 226	13, 16, 17	57
Плинтус МДФ под покраску 80×16, крепление к стене, окраска в цвет Little Greene No. 105	14	10
SX165, h = 69 мм, крепление к стене, окраска в цвет Farrow & Ball No. 226	18, 19	37

Отметки по высоте

±0,000 чистый пол 1-го этажа; отсчёт отметок
+3,150 чистый пол пом. 13, 14, 16–19 (мансарда)
+3,135 чистый пол пом. 15, 20, ниже на 15 мм
+3,086 верх плиты — расчёт, не замер (задание на обмер)
сущ. пол снимается до плиты; не замерен (задание на обмер)


Примечания

1. За отметку ±0,000 принят чистый пол 1-го этажа, не существующий; чистый пол этажа +3,150 (блок отметок). Площади — по чистым размерам помещений, м²; размеры — в мм.
2. Стык разнотипных покрытий — по оси дверного полотна (под полотном в закрытом положении); решение стыка — по ведомости стыков.
3. Пол санузлов ниже смежных помещений на 15 мм за счёт меньшей толщины стяжки (верх плиты общий — по экспликации полов); гидроизоляция по стяжке с заведением на стены не менее 200 мм (СП 29.13330.2011, п. 7.2), до облицовки — тест проливом и акт скрытых работ.
4. Трубопроводы в конструкции пола не прокладываются: пирог пола 49–64 мм не вмещает выпуски канализации с уклоном — выпуски К1 ведутся по стенам над чистым полом в коробах.
5. Штучные покрытия (инженерная доска): направление — по стрелке; влажность основания по СМ не более 2,0 % (по ТУ изготовителя).
6. Ровность основания — просвет под 2-метровой рейкой не более 2 мм: пом. 13, 14, 16, 17, 18, 19 (инженерная доска), пом. 15, 20 (керамогранит); проверить до укладки покрытия (СП 71.13330.2017, табл. 8.5).
7. Сетка на плитке — условная, в размер формата; точка старта и раскладка — по листу раскладки плитки.
8. Узор покрытия (заливка-код типа пола) прерывается под надписями — площадями помещений и отметками чистого пола.
9. Пироги полов — по экспликации полов: слои сверху вниз, толщины в мм; гидроизоляция мокрых зон — в пироге и в ведомости отделки; схема пола — без масштаба.


					Проект: Дом 331 м² — **М 1:75**
	Лист	№ док.	Подпись	Дата	
Дизайнер	Кырлан А.С.			04.11.26	План покрытий пола · Мансарда
					Стадия: П; Лист: 74; Листов: 168

выпуск 04.11.2026 № f163a372b2 · стр. 74 из 168


Фрагмент 1. Санузел 1 этажа (пом. 3). Пол 600×600, шов 2 мм, М 1:50

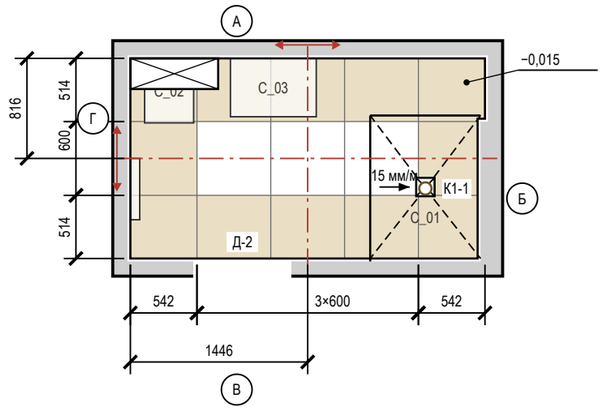

Фрагмент 2. Санузел мастер (пом. 15). Пол 600×600, шов 2 мм, М 1:50

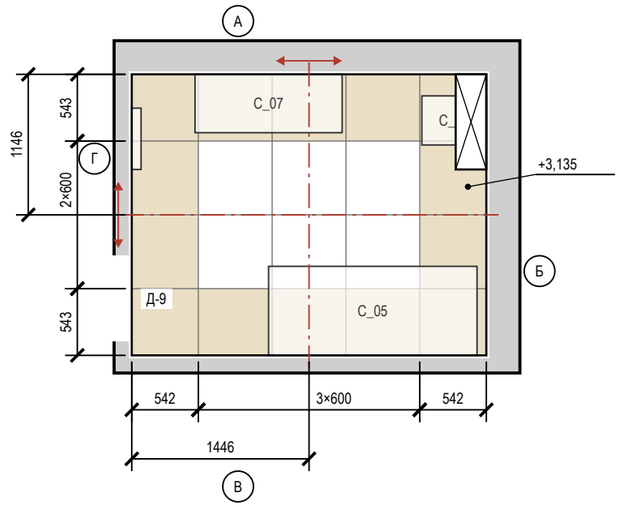

Фрагмент 3. Санузел 2 (пом. 20). Пол 600×600, шов 2 мм, М 1:50

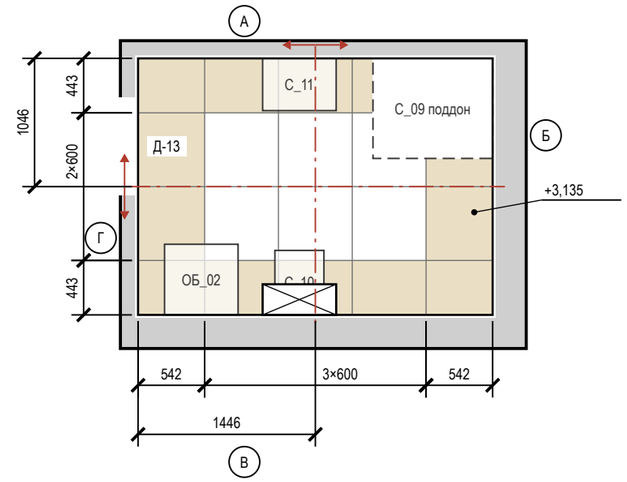

Ведомость материалов

Материал	Класс, код	Норма расхода	Кол-во
Затирка	CG2WA Mapei Ultracolor Plus 132	(a+b)/ab·шов·t·1,6	7,1 кг
Затирка	CG2WA	(a+b)/ab·шов·t·1,6	3,9 кг
Клей	C2 TE S1 Ceresit CM 17	1,5 кг/м²·мм, слой 5	691 кг (28 меш.)
Клей	C2 TE S1	1,5 кг/м²·мм, слой 5	389 кг (16 меш.)
Гидроизоляция	обмазочная, 2 слоя: пол, стены по периметру и зоны замачивания	по ТУ	44,9 м²
Демпф. лента	по периметру пола из плитки		90,5 м

Ведомость плитки

Помещение, поверхность	Плитка, код	Формат	Шов	S, м²	Целых	Подр.	С запасом
Санузел 1 этажа, пол	аналог: керамогранит под травертин	600×600	2	4,87	3	14	19
Санузел 1 этажа, стены А–Г	A8UZ	600×1200	2	19,67	11	19	34
Санузел 1 этажа, короб инсталляции	A8UZ	600×1200	2	1,64	0	6	7
Санузел мастер, пол	аналог: керамогранит под травертин	600×600	2	6,88	6	14	22
Санузел мастер, стены А–Г	A8UZ	600×1200	2	19,01	14	21	39
Санузел мастер, короб инсталляции	A8UZ	600×1200	2	1,73	0	6	7
Санузел 2, пол	аналог: керамогранит под травертин	600×600	2	6,29	5	14	21
Санузел 2, стены А–Г	A8UZ	600×1200	2	17,04	14	21	39
Санузел 2, короб инсталляции	A8UZ	600×1200	2	1,47	1	3	5
Котельная, пол	A8UZ	600×1200	2	6,88	0	10	11
Прихожая, пол	A8UZ	600×1200	2	12,46	3	16	21
Тамбур, пол	A8UZ	600×1200	2	3,49	0	6	7
Веранда, пол	A8UZ	600×1200	2	21,84	13	32	50
Крыльцо, пол	A8UZ	600×1200	2	3,38	0	6	7
Итого 600×600				18,04	14	42	62
Итого 600×1200				**108,60**	**56**	**146**	**227**

Условные обозначения

- плитка целая; тонкая линия — шов
- плитка с подрезкой (размер — на цепочке)
- ось старта; стрелки — направление укладки
- сантехприбор: габарит, высота по практике
- поддон душа — плитку пола под ним не кладут
- короб инсталляции: плитка пола — до короба
- трап / лоток в полу
- направление уклона К1 / пола: Ø, мм на 1 м
- край подиума; штрих — конверт к трапу
- вывод К1 (код — в ведомости привязок)
- отметка чистого пола на полке выноски, м
- А — обозначение стены А–Г (как на развёртках)

Примечания

1. Раскладка от чистовых размеров: стены санузлов теряют 10 + 5 + 9 = 24 мм на сторону (штукатурка, клей, плитка); подрезки — чистые, без шва.
2. Старт — от центра помещения (штрихпунктир, стрелки — направление укладки); размер старта — от чистовых стен Г и А.
3. Раскладка пола «Котельная» и пола «Прихожая» и пола «Тамбур» и пола «Веранда» и пола «Крыльцо» — на листе «Раскладка плитки. Котельная. Прихожая. Тамбур. Веранда. Крыльцо».
4. Калибр партии не задан — до укладки замерить (рабочий размер W, ГОСТ 13996-2019) и пересчитать подрезки.
5. Количество: целые по раскладке + по одной на подрезку, запас 10 %; один артикул — одна партия и тон. Исключены поддон, короб, проёмы и места за коробом; S — по чистым граням: стены нетто = зона облицовки по ведомости отделки − место за коробом инсталляции 2,51 м² (плитку за коробом не кладут), короб — отдельной строкой.
6. Клей C2 TE S1 Ceresit CM 17; C2 TE S1 (ГОСТ Р 56387-2018), затирка CG2WA Mapei Ultracolor Plus 132; CG2WA; расход — по ТУ выбранной марки.
7. Гидроизоляция: пол и стены 200 мм от ЧП; у душа — на всю высоту стен душевой зоны и 500 мм за край душевой зоны (пом. 3), над ванной — до 2000 и 300 мм за борт (пом. 15), у душа до 2000 и 500 мм за поддон (пом. 20) (см. развёртки); акт скрытых работ, пролив 24 ч.
8. Подиум душа С_01 (пом. 3): h 100 у трапа, решётка +0,085; верх — плиткой пола той же раскладки, уклон 15 мм/м к трапу, подрезка по линиям конверта; ступень по краю 109, грань 900 × 109 + 1166 × 107 = 0,22 м² (+2 шт. в подрезках), угол — профилем; гидроизоляция 2 сл. — по плите под подиумом, по верху и грани (узел 1 ВК); предложение, до согласования не выполнять.
9. Швы пола совмещены со швами стены А; по периметру — демпферная лента.
10. Отметка чистого пола −0,015, +3,135, порог 15 мм; стык с соседним покрытием — по оси полотна двери.


	Лист	№ док.	Подпись	Дата
Дизайнер	Кырлан А.С.			04.11.26

Проект: Дом 331 м² — **М 1:50**


Раскладка плитки. Планы полов

Стадия	Лист	Листов
П	75	168


Фрагмент 1. Котельная (пом. 4). Пол 600×1200, шов 2 мм, М 1:40

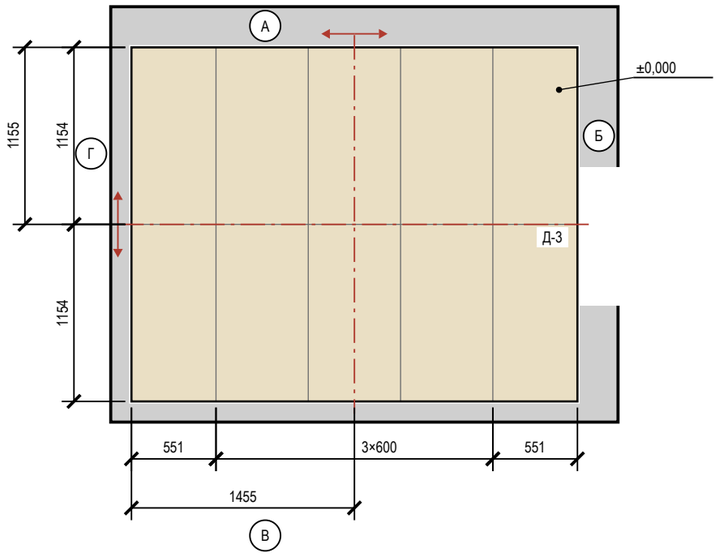

Фрагмент 2. Прихожая (пом. 8). Пол 600×1200, шов 2 мм, М 1:40

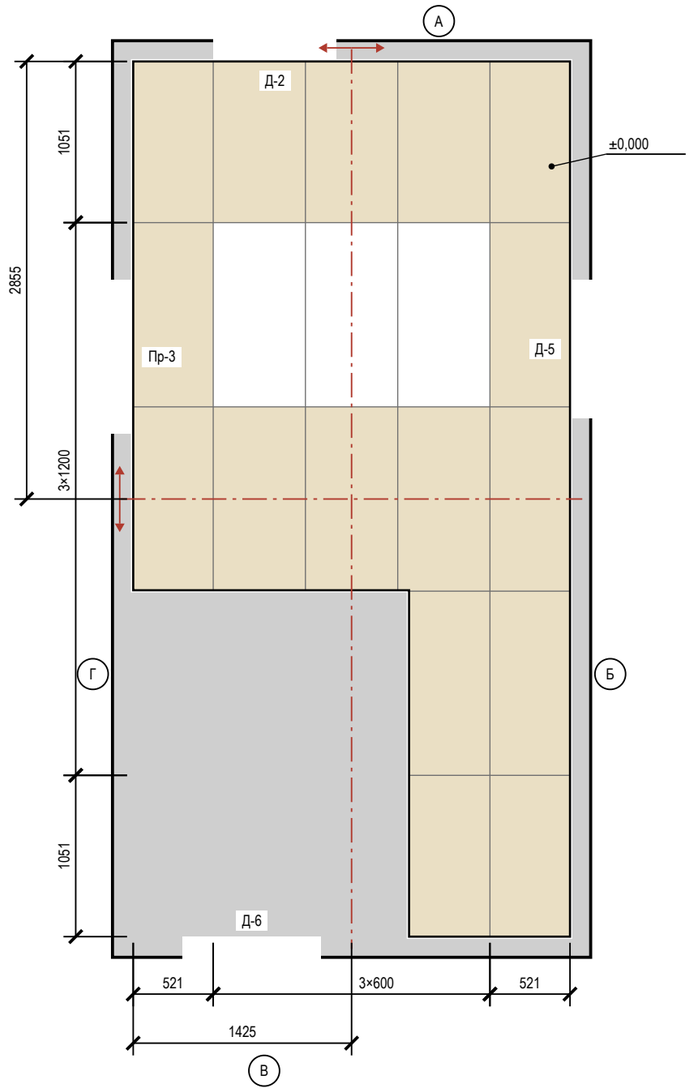

Фрагмент 3. Тамбур (пом. 9). Пол 600×1200, шов 2 мм, М 1:40

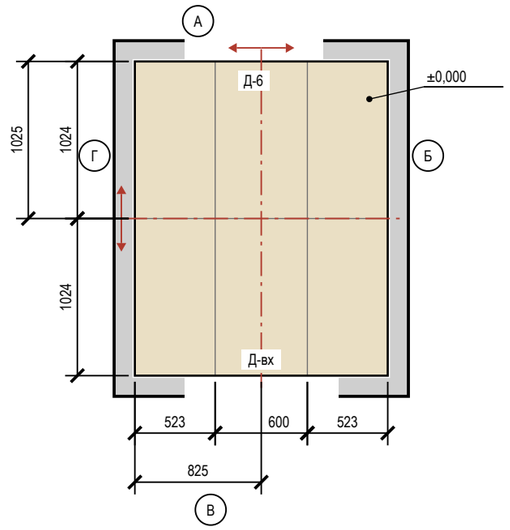

Условные обозначения

- плитка целая; тонкая линия — шов
- плитка с подрезкой (размер — на цепочке)
- ось старта; стрелки — направление укладки
- отметка чистого пола на полке выноски, м
- (А) обозначение стены А–Г (как на развёртках)

Подсчёт плитки

Поверхность	Формат	S, м²	Целых	Подр.	С запасом
Котельная, пол	600×1200	6,88	0	10	11
Прихожая, пол	600×1200	12,46	3	16	21
Тамбур, пол	600×1200	3,49	0	6	7

Примечания

1. Котельная: керамогранит 600×1200, длинная сторона — вдоль стен Б и Г, шов 2 мм, прямая раскладка от центра. Стены окрашены: раскладка от чистового контура минус штукатурка и шпаклёвка 15 мм на сторону (принято); подрезки 551 / 1154 мм, срез — под плинтус.
2. Котельная: деформационный зазор по периметру 8–10 мм под плинтусом; в проёмах — стык с соседним покрытием по оси полотна двери. Клей C2 TE S1, затирка CG2WA.
3. Прихожая: керамогранит 600×1200, длинная сторона — вдоль стен Б и Г, шов 2 мм, прямая раскладка от центра. Стены окрашены: раскладка от чистового контура минус штукатурка и шпаклёвка 15 мм на сторону (принято); подрезки 521 / 1051 мм, срез — под плинтус.
4. Прихожая: деформационный зазор по периметру 8–10 мм под плинтусом; в проёмах — стык с соседним покрытием по оси полотна двери. Клей C2 TE S1, затирка CG2WA.
5. Тамбур: керамогранит 600×1200, длинная сторона — вдоль стен Б и Г, шов 2 мм, прямая раскладка от центра. Стены окрашены: раскладка от чистового контура минус штукатурка и шпаклёвка 15 мм на сторону (принято); подрезки 523 / 1024 мм, срез — под плинтус.
6. Тамбур: деформационный зазор по периметру 8–10 мм под плинтусом; в проёмах — стык с соседним покрытием по оси полотна двери. Клей C2 TE S1, затирка CG2WA.
7. Клей, затирка и итог по форматам — в ведомостях листа «Раскладка плитки. Планы полов».

					Проект: Дом 331 м²	М 1:40
	Лист	№ док.	Подпись	Дата		
Дизайнер	Кырлан А.С.			04.11.26	Раскладка плитки. Котельная. Прихожая. Тамбур	Стадия / Лист / Листов
						П / 76 / 168

выпуск 04.11.2026 № f163a372b2 · стр. 76 из 168

Развёртка стены А


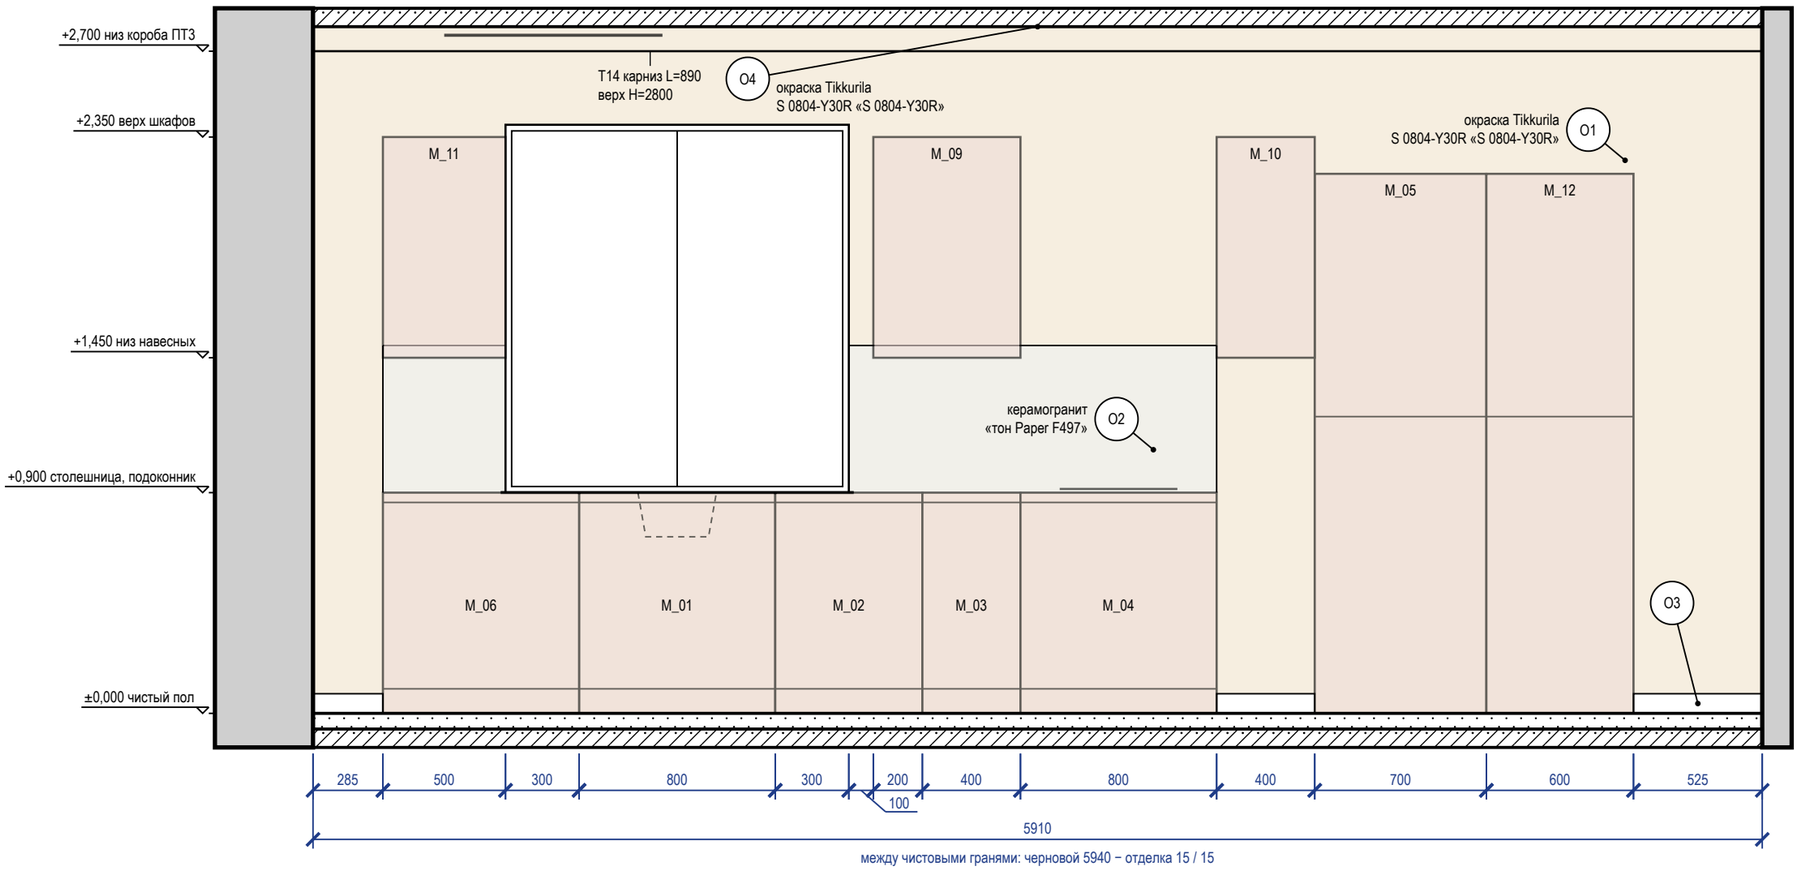


Схема развёрток (М 1:100)

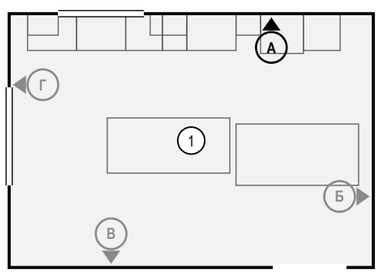

Ведомость отделки (на листе)

Марка	Поверхность	Материал, изделие	Цвет, код	Кол.
O1	стены	окраска, Tikkurila Luja 7, шелковисто-матовая, подготовка К3	NCS S 0804-Y30R «S 0804-Y30R»	12,4 м²
O2	фартук	керамогранит, аналог: керамогранит матовый, тон F497, затирка CG2WA	#F1F1EC «тон Paper F497»	1,2 м²
O3	плинтус	плинтус МДФ, h 80 мм, аналог: плинтус МДФ под окраску 80×16 мм, полуглянцевая	NCS S 0804-Y30R «S 0804-Y30R»	1,2 м
O4	потолок	окраска, Tikkurila Luja 7, матовая, подготовка Q3	NCS S 0804-Y30R «S 0804-Y30R»	24,6 м²

Примечания

1. Размеры — в мм от чистовых поверхностей стен; условные обозначения и общие указания — лист 3.
2. Стена А показана двумя видами: здесь — архитектурная развёртка (мебель, отделка, проёмы, высоты), электроточки и выводы ВК с привязками и таблицей — на листе 78 («Привязки»).
3. Карнизы (шины) — по ведомости текстиля декоратора: длина L и верх H на развёртке — те же числа, что в ведомости; крепление — до окраски потолка.
4. Потолок — у каждой стены свой, по плану потолков (НШ1, ПТ3); ступени — зоной, кромка короба перед нишей — тонкой линией; в поле потолка: ПТ1 +2,550, ПТ2 +2,600.

					Проект: Дом 331 м²	М 1:25
	Лист	№ док.	Подпись	Дата	Развёртка стены А. Кухня-столовая (пом. 1), кухонный фронт	Стадия / Лист / Листов
Дизайнер	Кырлан А.С.			04.11.26		П / 77 / 168

Развёртка стены А: электроточки и выводы

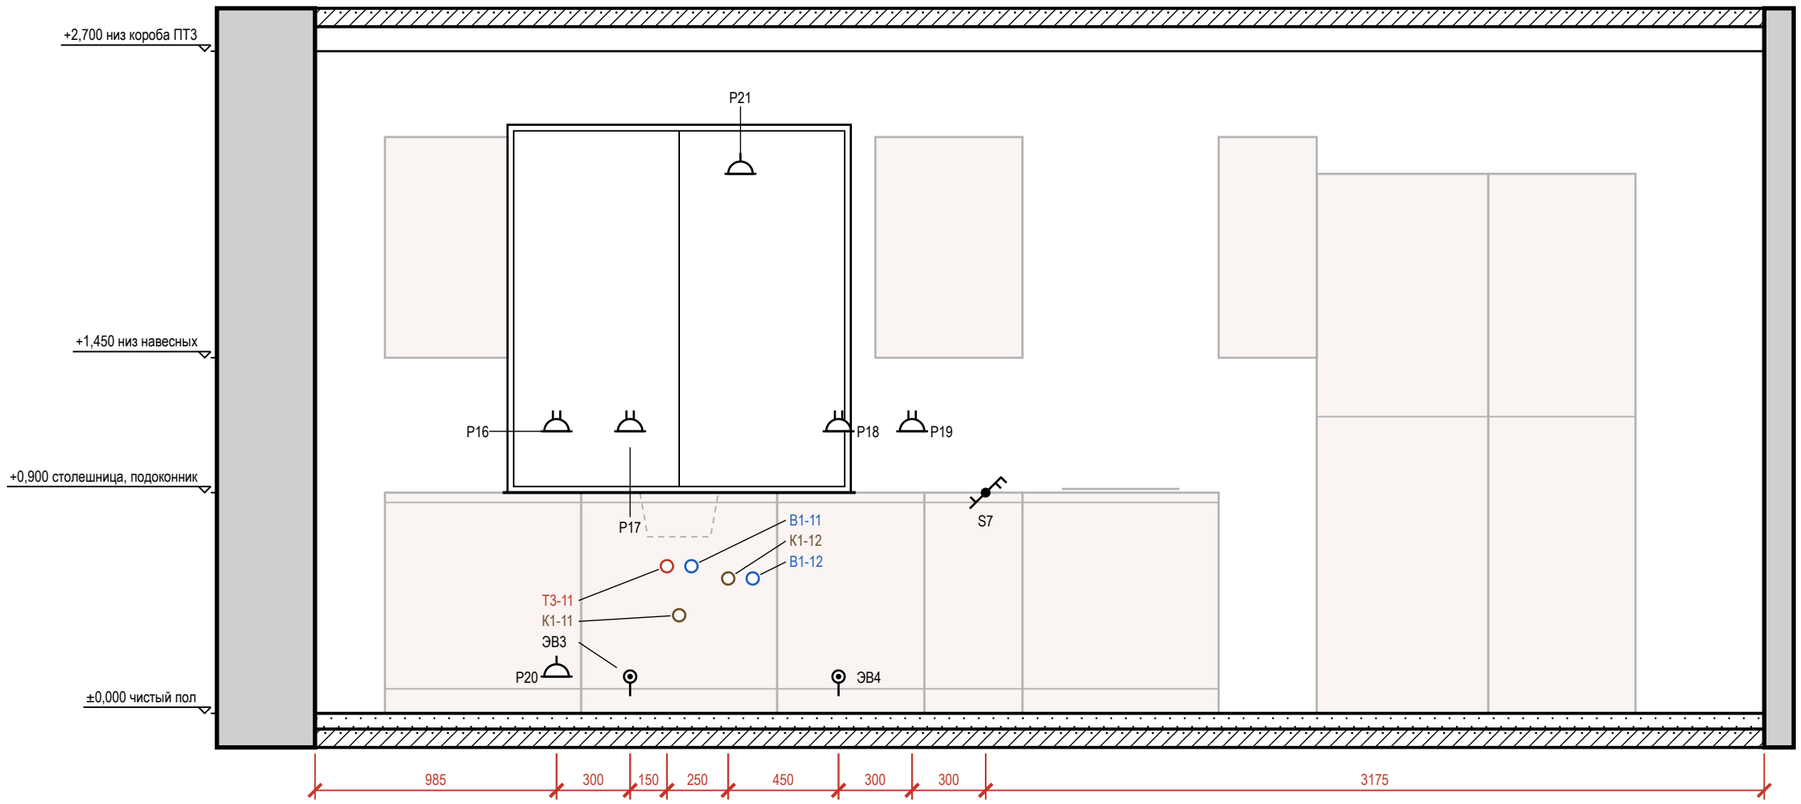


Таблица привязок электроточек и выводов

Марка	Назначение	От угла, мм	H от пола, мм	Примечание
P20	розетка: холодильник встроенный M_05 (розетка в соседнем модуле)	985	150	гр. 10
P16	розетка: фартук: мелкая техника	985	1150	рамка 2 поста, гр. 9
ЭВ3	вывод кабеля: варочная панель M_04	1285	150	гр. 11
P17	розетка: фартук: мелкая техника	1285	1150	рамка 2 поста, гр. 9
T3-11	горячая вода — мойка кухонная	1435	600	межос. 100
K1-11	канализация — мойка кухонная	1485	400	Ø50
B1-11	холодная вода — мойка кухонная	1535	600	межос. 100

Марка	Назначение	От угла, мм	H от пола, мм	Примечание
K1-12	канализация — посудомоечная машина	1685	550	Ø40; слив ПММ в шкафу мойки
P21	розетка: вытяжка над варочной панелью M_04 (розетка за съёмной панелью)	1735	2200	гр. 10
B1-12	холодная вода — посудомоечная машина	1785	550	кран ПММ в шкафу мойки
ЭВ4	вывод кабеля: духовой шкаф M_04 (вывод в соседнем модуле)	2135	150	гр. 15
P18	розетка: фартук: мелкая техника	2135	1150	рамка 2 поста, гр. 9
P19	розетка: фартук: мелкая техника	2435	1150	рамка 2 поста, гр. 9
S7	выключатель	2735	900	гр. 1

Условные обозначения

- розетка с заземляющим контактом; у знака — марка, ×N постов в рамке, гр. — группа щита, H — высота оси, мм
- вывод кабеля для подключения прибора (без розетки), марка ЭВ
- выключатель одноклавишный
- выключатель двухклавишный (флажков — по числу клавиш)
- выключатель с проходной или перекрёстной клавишей (обратный флажок); тип клавиши — в подписи
- вывод B1 (код — в ведомости привязок)
- вывод T3 (код — в ведомости привязок)
- вывод K1 (код — в ведомости привязок)
- привязки точек и выводов от угла и от пола, мм

Примечания

1. Вид «Привязки» стены А — электроточки и выводы ВК; архитектурная развёртка (мебель, отделка, проёмы, высоты) — на листе 77. Мебель и приборы — подложкой для ориентира; их марки и обозначения мебели, проёмов и стен — там же.
2. Привязки — в мм: по горизонтали от левого чистового угла стены до оси изделия, H — от чистого пола до оси; все точки — в таблице привязок. Красная цепочка — привязки по осям; точки ближе 150 мм одна к другой в цепочку не дробятся — их привязки только в таблице.
3. У знака — марка электроточки (P — розетка, S — выключатель, Св — светильник, ЭВ — вывод кабеля); условные обозначения и общие указания — лист 3.
4. Коды выводов ВК: B1 — холодная вода, T3 — горячая вода, K1 — канализация; номер после дефиса — номер вывода на листе выводов сантехники.
5. Выводы кухонной техники — по утверждённому проекту кухни: привязки выводов даются от осей модулей гарнитура.

					Проект: Дом 331 м²	М 1:25
	Лист	№ док.	Подпись	Дата	Привязки электроточек и выводов ВК, стена А. Кухня-столовая (пом. 1)	Стадия / Лист / Листов
Дизайнер	Кырлан А.С.			04.11.26		П / 78 / 168

Развёртка стены Б


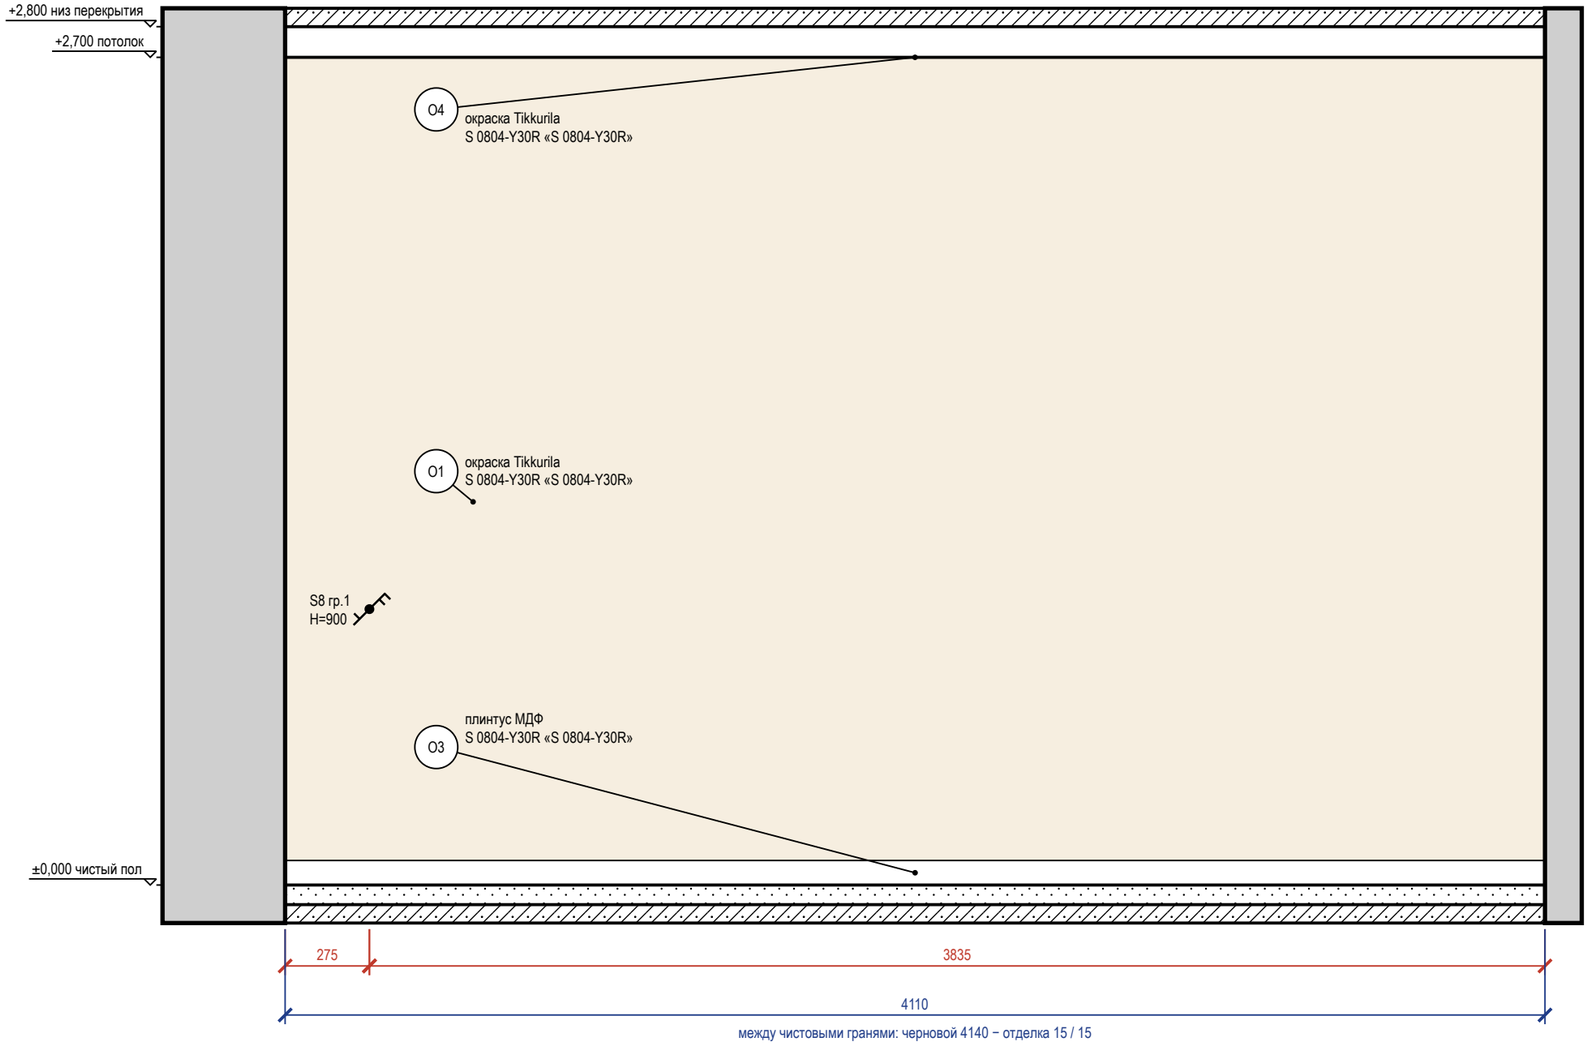


Схема развёрток (М 1:100)

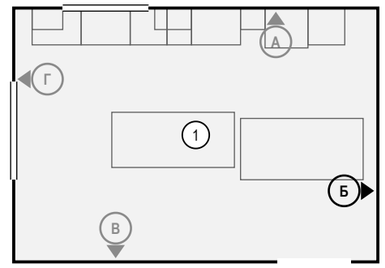

Ведомость отделки (на листе)

Марка	Поверхность	Материал, изделие	Цвет, код	Кол.
О1	стены	окраска, Tikkurila Luja 7, шелковисто-матовая, подготовка К3	NCS S 0804-Y30R «S 0804-Y30R»	11,1 м²
О3	плинтус	плинтус МДФ, h 80 мм, аналог: плинтус МДФ под окраску 80×16 мм, полуглянцевая	NCS S 0804-Y30R «S 0804-Y30R»	4,1 м
О4	потолок	окраска, Tikkurila Luja 7, матовая, подготовка Q3	NCS S 0804-Y30R «S 0804-Y30R»	24,6 м²

Примечания

1. Размеры — в мм от чистовых поверхностей стен; условные обозначения и общие указания — лист 3.
2. Потолок — у каждой стены свой, по плану потолков (ПТ3); ступени — зоной, кромка короба перед нишей — тонкой линией; в поле потолка: ПТ1 +2,550, ПТ2 +2,600.


	Лист	№ док.	Подпись	Дата
Дизайнер	Кырлан А.С.			04.11.26

Проект: Дом 331 м² — **М 1:20**

Развёртка стены Б. Кухня-столовая (пом. 1)


Стадия	Лист	Листов
П	79	168

Развёртка стены В

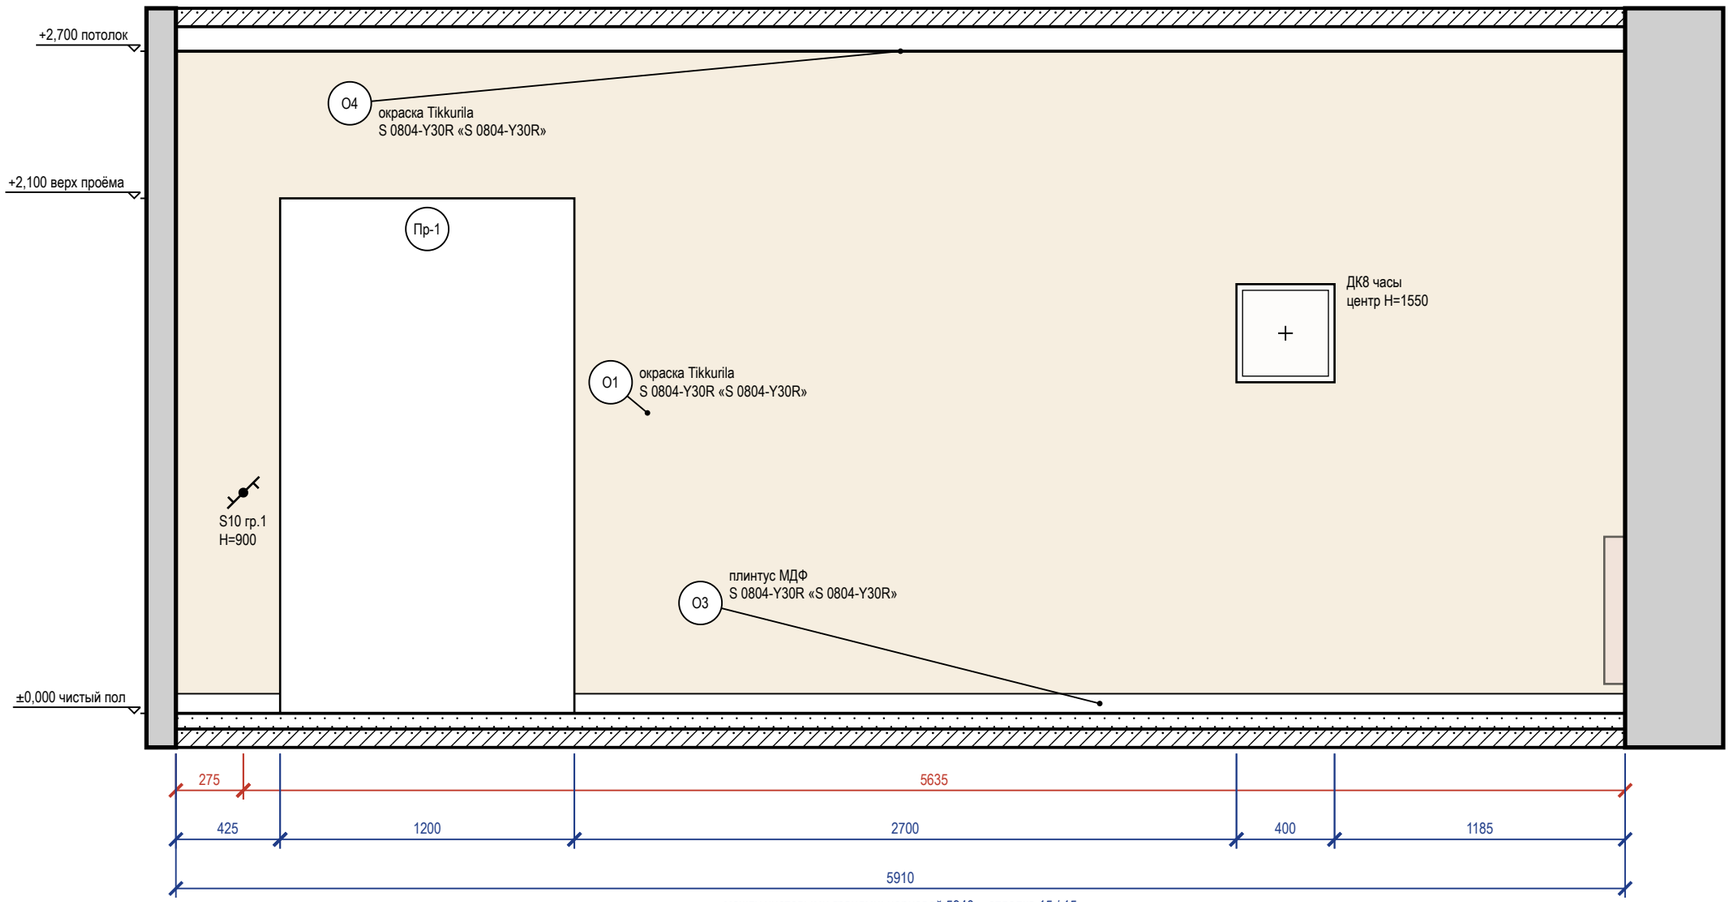

между чистовыми гранями: черновой 5940 − отделка 15 / 15

Схема развёрток (М 1:100)

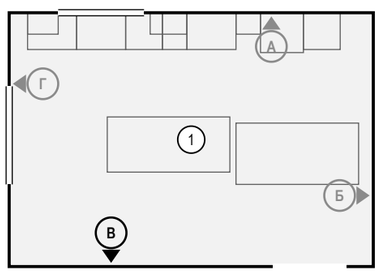

Ведомость отделки (на листе)

Марка	Поверхность	Материал, изделие	Цвет, код	Кол.
О1	стены	окраска, Tikkurila Luja 7, шелковисто-матовая, подготовка К3	NCS S 0804-Y30R «S 0804-Y30R»	13,4 м²
О3	плинтус	плинтус МДФ, h 80 мм, аналог: плинтус МДФ под окраску 80×16 мм, полуглянцевая	NCS S 0804-Y30R «S 0804-Y30R»	4,7 м
О4	потолок	окраска, Tikkurila Luja 7, матовая, подготовка Q3	NCS S 0804-Y30R «S 0804-Y30R»	24,6 м²

Примечания

1. Размеры — в мм от чистовых поверхностей стен; условные обозначения и общие указания — лист 3.
2. Картины и зеркала крепить к основанию по паспорту изделия (закладные и анкеры — в перечне скрытых работ); крест — ось центра предмета.
3. Потолок — у каждой стены свой, по плану потолков (ПТ3); ступени — зоной, кромка короба перед нишей — тонкой линией; в поле потолка: ПТ1 +2,550, ПТ2 +2,600.

					Проект: Дом 331 м²	М 1:25
	Лист	№ док.	Подпись	Дата	Развёртка стены В. Кухня-столовая (пом. 1)	Стадия / Лист / Листов
Дизайнер	Кырлан А.С.			04.11.26		П / 80 / 168

выпуск 04.11.2026 № f163a372b2 · стр. 80 из 168

Развёртка стены Г


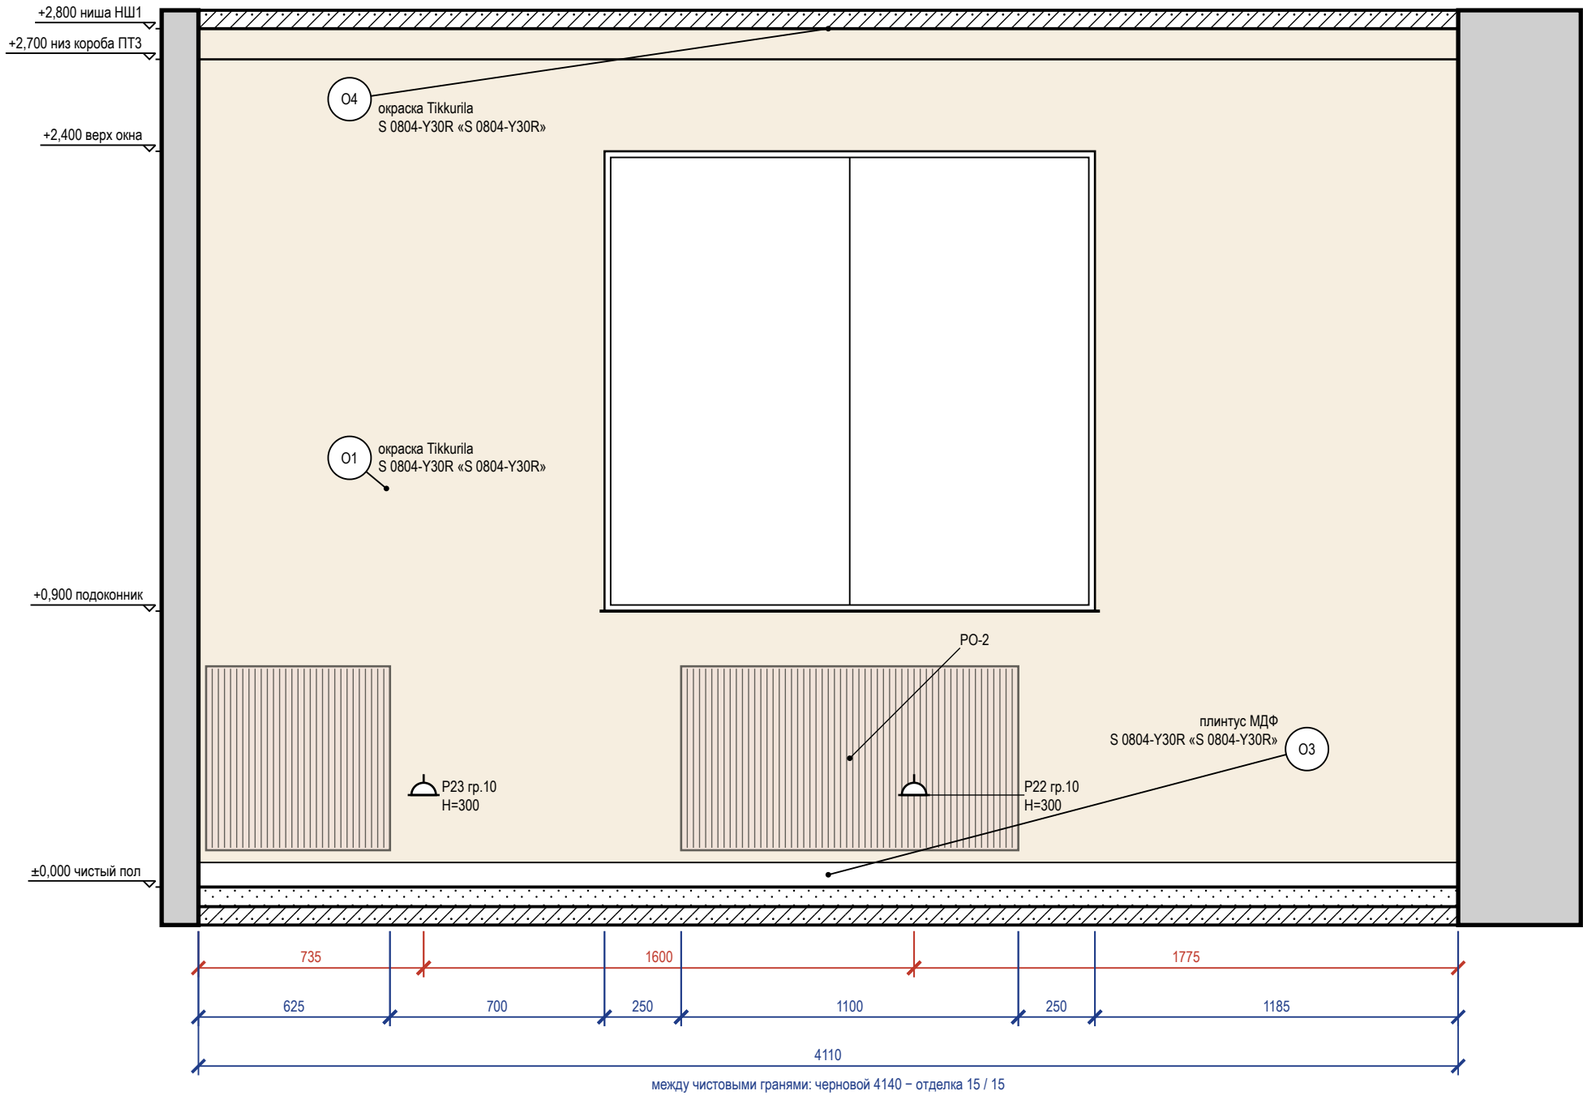


Схема развёрток (М 1:100)

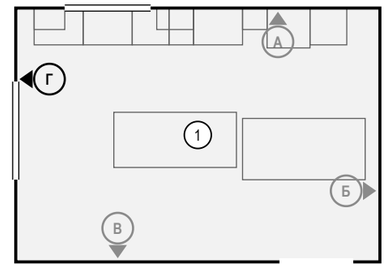

Ведомость отделки (на листе)

Марка	Поверхность	Материал, изделие	Цвет, код	Кол.
О1	стены	окраска, Tikkurila Luja 7, шелковисто-матовая, подготовка К3	NCS S 0804-Y30R «S 0804-Y30R»	9,1 м²
О3	плинтус	плинтус МДФ, h 80 мм, аналог: плинтус МДФ под окраску 80×16 мм, полуглянцевая	NCS S 0804-Y30R «S 0804-Y30R»	4,1 м
О4	потолок	окраска, Tikkurila Luja 7, матовая, подготовка Q3	NCS S 0804-Y30R «S 0804-Y30R»	24,6 м²

Примечания

1. Размеры — в мм от чистовых поверхностей стен; условные обозначения и общие указания — лист 3.
2. Потолок — у каждой стены свой, по плану потолков (НШ1, ПТ3); ступени — зоной, кромка короба перед нишей — тонкой линией; в поле потолка: ПТ1 +2,550, ПТ2 +2,600.

					Проект: Дом 331 м² — М 1:20
	Лист	№ док.	Подпись	Дата	Развёртка стены Г. Кухня-столовая (пом. 1)
Дизайнер	Кырлан А.С.			04.11.26	

Стадия	Лист	Листов
П	81	168

Развёртка стены А


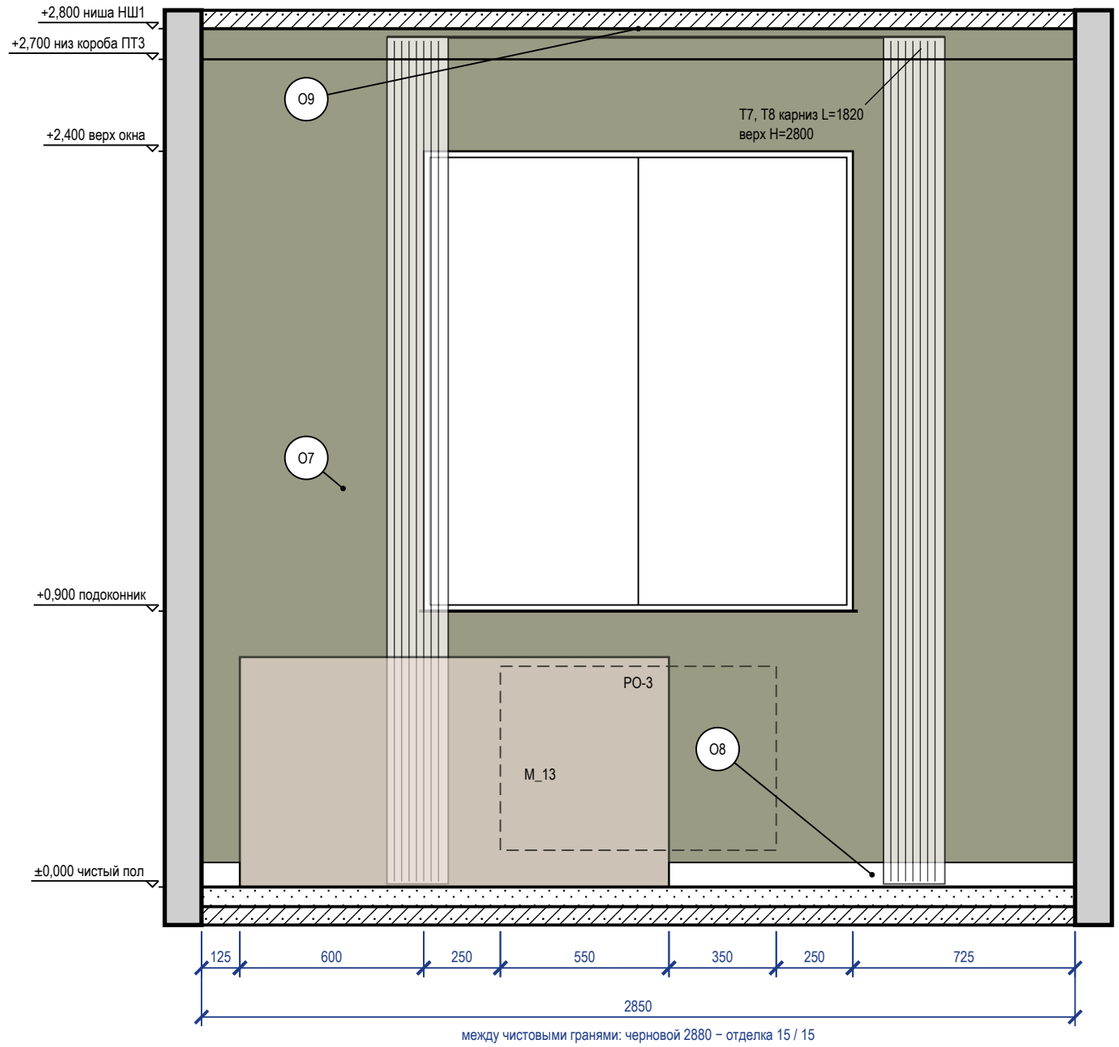


Схема развёрток (М 1:100)

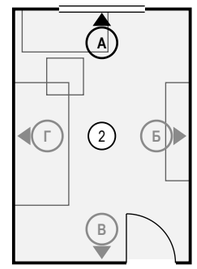

Ведомость отделки (на листе)

Марка	Поверхность	Материал, изделие	Цвет, код	Кол.
О7	акцентная стена	окраска, Farrow & Ball Modern Emulsion, матовая, подготовка Q3	Farrow & Ball No. 298 «Bancha»	5,9 м²
О8	плинтус	плинтус МДФ, h 80 мм, аналог: плинтус МДФ под покраску 80×16	Farrow & Ball No. 226 «Joa's White»	1,4 м
О9	потолок	окраска, Little Greene Absolute Matt, глубокоматовая, подготовка Q3	Little Greene No. 105 «Slaked Lime»	11,9 м²

Примечания

1. Размеры — в мм от чистовых поверхностей стен; условные обозначения и общие указания — лист 3.
2. Стена А показана двумя видами: здесь — архитектурная развёртка (мебель, отделка, проёмы, высоты), электроточки и выводы ВК с привязками и таблицей — на листе 85 («Привязки»).
3. Карнизы (шины) — по ведомости текстиля декоратора: длина L и верх H на развёртке — те же числа, что в ведомости; крепление — до окраски потолка.
4. Потолок — у каждой стены свой, по плану потолков (НШ1, ПТ3); ступени — зоной, кромка короба перед нишей — тонкой линией; в поле потолка: ПТ2 +2,600.

					Проект: Дом 331 м²	М 1:20
	Лист	№ док.	Подпись	Дата		
Дизайнер	Кырлан А.С.			04.11.26	Развёртка стены А. Кабинет-гостевая (пом. 2)	Стадия: П; Лист: 82; Листов: 168

Развёртка стены Б


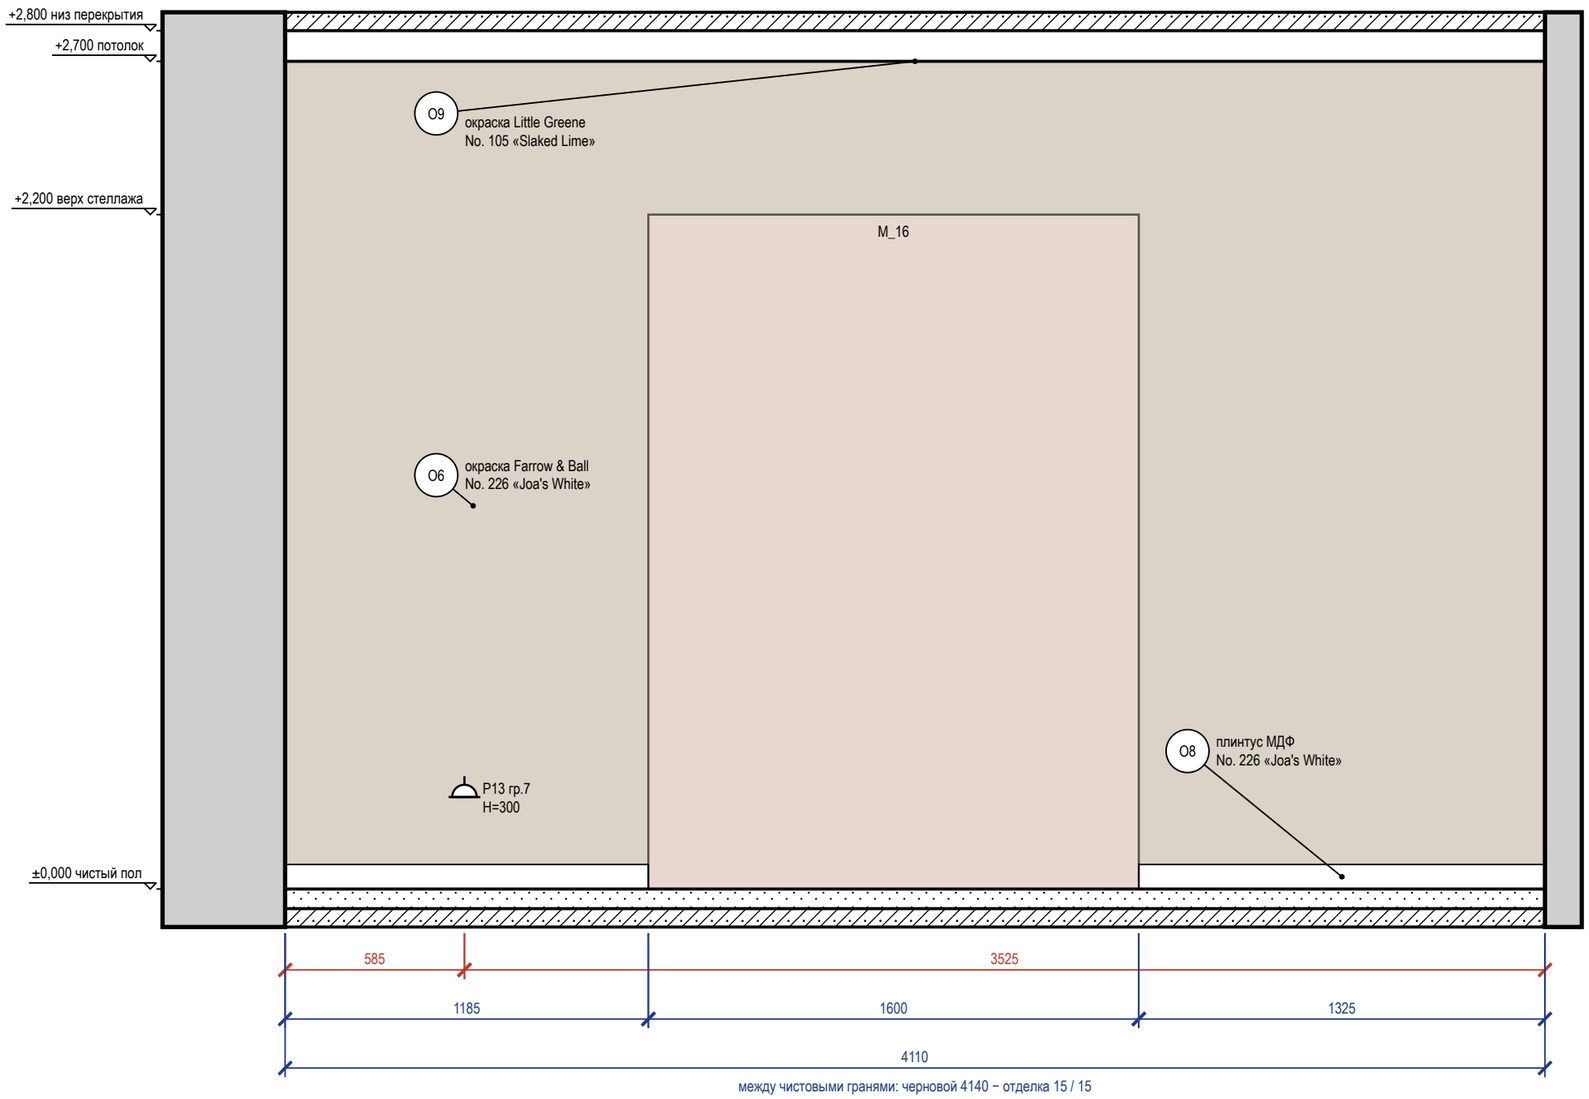


Схема развёрток (М 1:100)

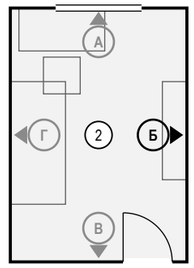

Ведомость отделки (на листе)

Марка	Поверхность	Материал, изделие	Цвет, код	Кол.
O6	стены	окраска, Farrow & Ball Modern Emulsion, матовая, подготовка Q3	Farrow & Ball No. 226 «Joa's White»	11,1 м²
O8	плинтус	плинтус МДФ, h 80 мм, аналог: плинтус МДФ под покраску 80×16	Farrow & Ball No. 226 «Joa's White»	2,5 м
O9	потолок	окраска, Little Greene Absolute Matt, глубокоматовая, подготовка Q3	Little Greene No. 105 «Slaked Lime»	11,9 м²

Примечания

1. Размеры — в мм от чистовых поверхностей стен; условные обозначения и общие указания — лист 3.
2. Потолок — у каждой стены свой, по плану потолков (ПТ3); ступени — зоной, кромка короба перед нишей — тонкой линией; в поле потолка: ПТ2 +2,600.

					Проект: Дом 331 м²	М 1:20
	Лист	№ док.	Подпись	Дата	Развёртка стены Б. Кабинет-гостевая (пом. 2)	Стадия / Лист / Листов
Дизайнер	Кырлан А.С.			04.11.26		П / 83 / 168

Развёртка стены В


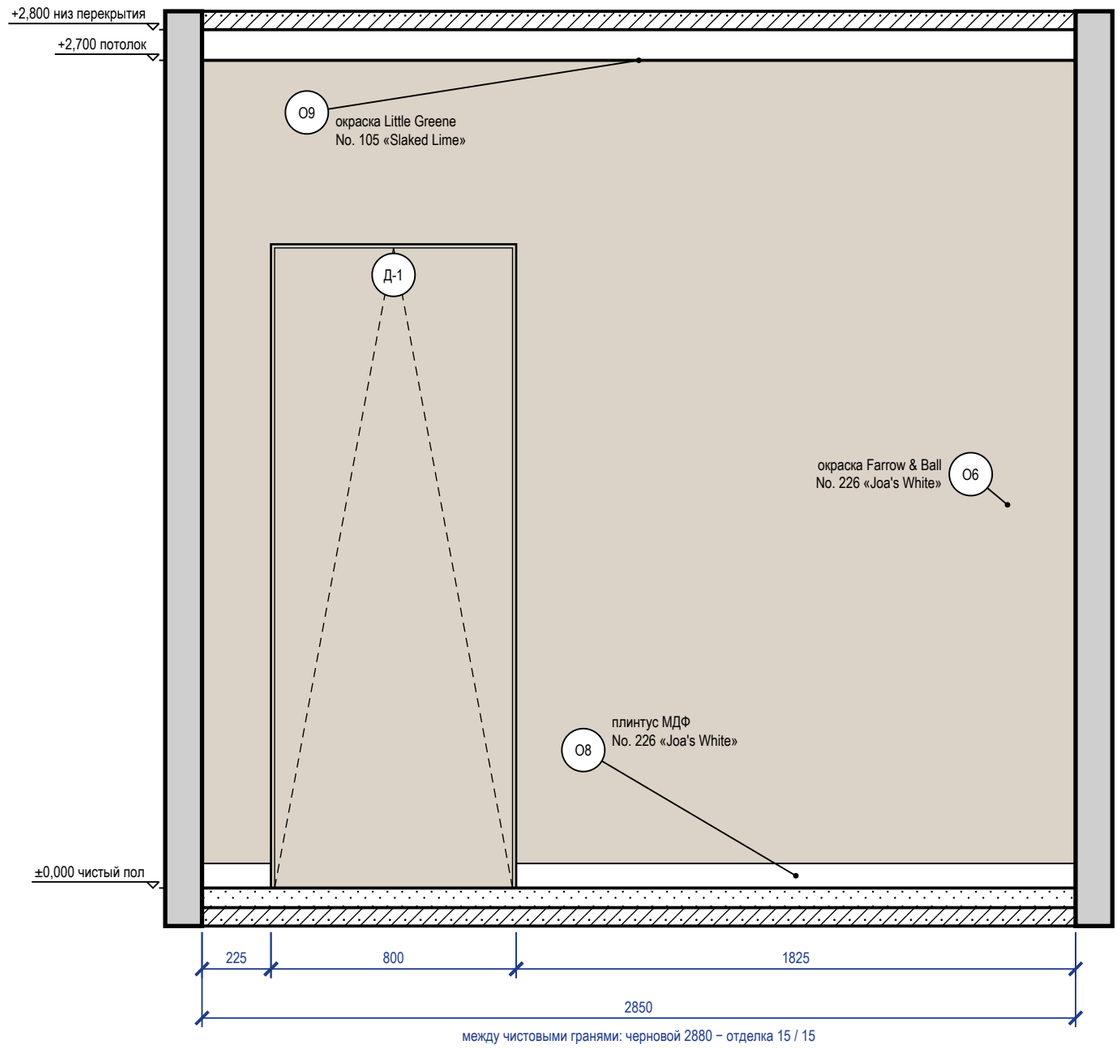


Схема развёрток (М 1:100)

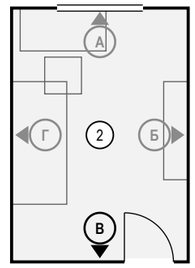

Ведомость отделки (на листе)


Марка	Поверхность	Материал, изделие	Цвет, код	Кол.
О6	стены	окраска, Farrow & Ball Modern Emulsion, матовая, подготовка Q3	Farrow & Ball No. 226 «Joa's White»	6 м²
О8	плинтус	плинтус МДФ, h 80 мм, аналог: плинтус МДФ под покраску 80×16	Farrow & Ball No. 226 «Joa's White»	2 м
О9	потолок	окраска, Little Greene Absolute Matt, глубокоматовая, подготовка Q3	Little Greene No. 105 «Slaked Lime»	11,9 м²

Примечания

1. Размеры — в мм от чистовых поверхностей стен; условные обозначения и общие указания — лист 3.
2. Стена В показана двумя видами: здесь — архитектурная развёртка (мебель, отделка, проёмы, высоты), электроточки и выводы ВК с привязками и таблицей — на листе 85 («Привязки»).
3. Двери скрытого монтажа — полотно в плоскости стены, отделка стены по полотну, плинтус прерывается у короба (узел — на листе узлов).
4. Потолок — у каждой стены свой, по плану потолков (ПТ3); ступени — зоной, кромка короба перед нишей — тонкой линией; в поле потолка: ПТ2 +2,600.

					Проект: Дом 331 м²	М 1:20
	Лист	№ док.	Подпись	Дата		
Дизайнер	Кырлан А.С.			04.11.26	Развёртка стены В. Кабинет-гостевая (пом. 2)	Стадия: П; Лист: 84; Листов: 168

Развёртка стены А: электроточки и выводы

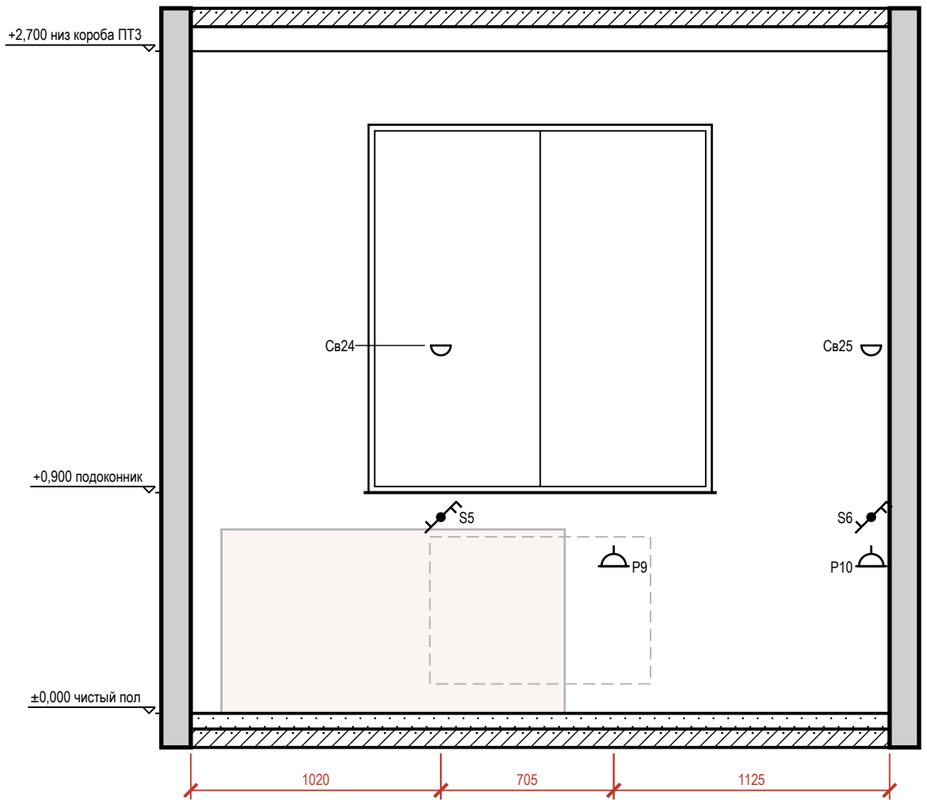

Развёртка стены В: электроточки и выводы

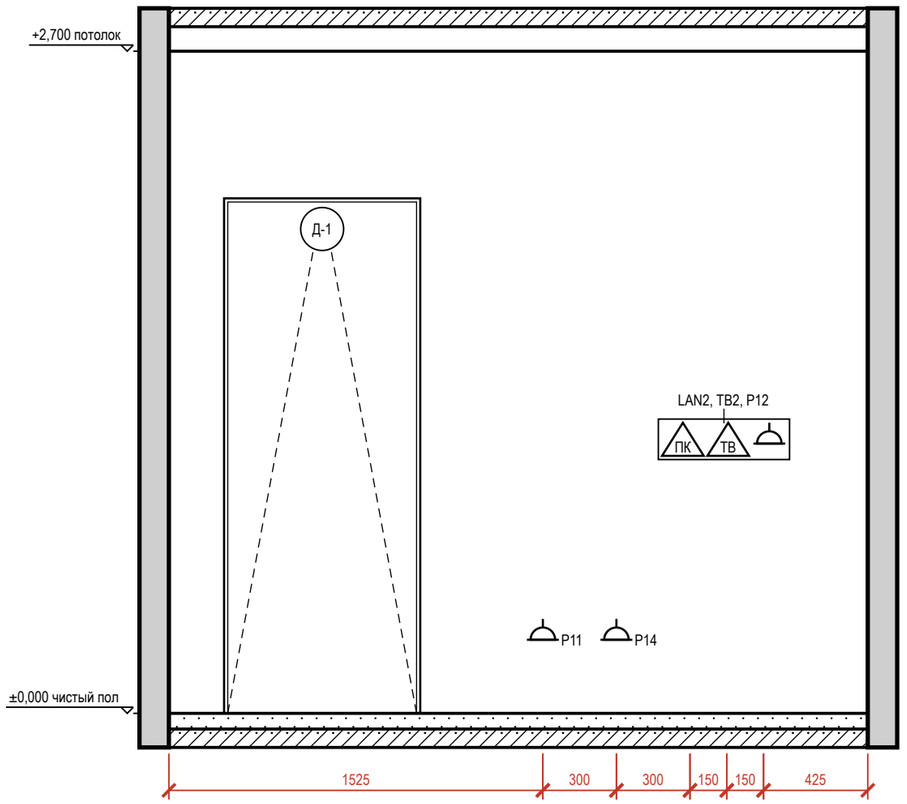



Таблица привязок электроточек и выводов

Стена	Марка	Назначение	От угла, мм	H от пола, мм	Примечание
A	S5	выключатель	1020	800	гр. 1
A	Св24	светильник настенный	1020	1500	гр. 1
A	P9	розетка: у кровати	1725	600	гр. 7
A	P10	розетка: у кровати	2775	600	гр. 7
A	S6	выключатель	2775	800	гр. 1
A	Св25	светильник настенный	2775	1500	гр. 1
B	P11	розетка: у комода	1525	300	гр. 7
B	P14	розетка: уборка у входа	1825	300	гр. 7
B	LAN2	розетка RJ45: Smart TV	2125	1100	
B	TB2	розетка ТВ: ТВ над комодом	2275	1100	
B	P12	розетка: ТВ над комодом (в одной зоне с TB2, LAN2)	2425	1100	гр. 7

Условные обозначения

- розетка с заземляющим контактом; у знака — марка, ×N постов в рамке, гр. — группа щита, H — высота оси, мм
- выключатель одноклавишный
- выключатель двухклавишный (флажков — по числу клавиш)
- выключатель с проходной или перекрёстной клавишей (обратный флажок); тип клавиши — в подписи
- светильник настенный (бра), H — высота оси
- ПК — розетка компьютерная RJ45
- ТВ — розетка телевизионная
- привязки точек и выводов от угла и от пола, мм
- A — марка развёртки: буква стены, стрелка — взгляд

Схема развёрток (М 1:100)

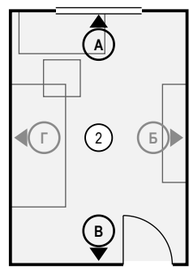

Примечания

1. Вид «Привязки» стен А, В — электроточки и выводы ВК; архитектурная развёртка (мебель, отделка, проёмы, высоты) — на листах 82, 84. Мебель и приборы подложкой для ориентира; их марки и обозначения мебели, проёмов и стен — там же.
2. Привязки — в мм: по горизонтали от левого чистового угла стены до оси изделия, H — от чистого пола до оси; все точки — в таблице привязок. Красная цепочка — привязки по осям; точки ближе 150 мм одна к другой в цепочку не дробятся — их привязки только в таблице.
3. У знака — марка электроточки (Р — розетка, S — выключатель, Св — светильник, ЭВ — вывод кабеля); условные обозначения и общие указания — лист 3.

					Проект: Дом 331 м²	М 1:25
	Лист	№ док.	Подпись	Дата	Привязки электроточек, стены А, В. Кабинет-гостевая (пом. 2)	Стадия / Лист / Листов
Дизайнер	Кырлан А.С.			04.11.26		П / 85 / 168

Развёртка стены Г


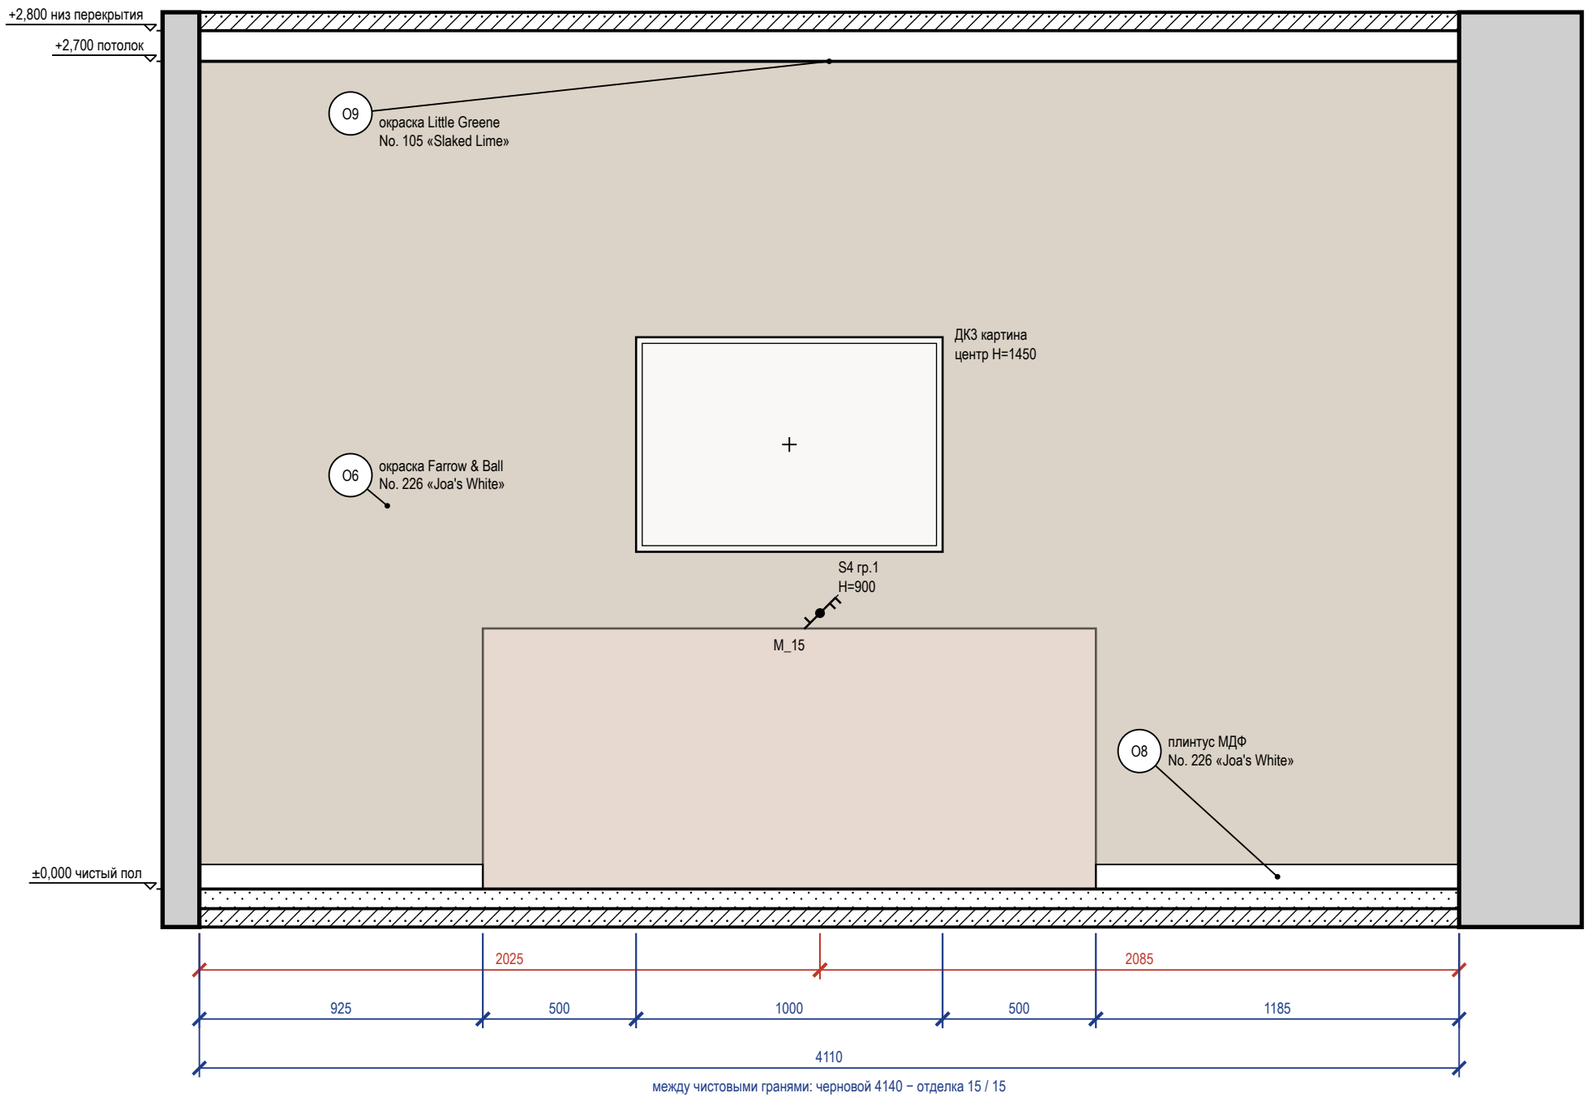


Схема развёрток (М 1:100)

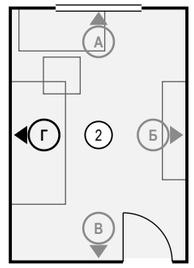

Ведомость отделки (на листе)


Марка	Поверхность	Материал, изделие	Цвет, код	Кол.
О6	стены	окраска, Farrow & Ball Modern Emulsion, матовая, подготовка Q3	Farrow & Ball No. 226 «Joa's White»	11,1 м²
О8	плинтус	плинтус МДФ, h 80 мм, аналог: плинтус МДФ под покраску 80×16	Farrow & Ball No. 226 «Joa's White»	2,1 м
О9	потолок	окраска, Little Greene Absolute Matt, глубокоматовая, подготовка Q3	Little Greene No. 105 «Slaked Lime»	11,9 м²

Примечания

1. Размеры — в мм от чистовых поверхностей стен; условные обозначения и общие указания — лист 3.
2. Картины и зеркала крепить к основанию по паспорту изделия (закладные и анкеры — в перечне скрытых работ); крест — ось центра предмета.
3. Потолок — у каждой стены свой, по плану потолков (ПТ3); ступени — зоной, кромка короба перед нишей — тонкой линией; в поле потолка: ПТ2 +2,600.

					Проект: Дом 331 м²	М 1:20
	Лист	№ док.	Подпись	Дата		
Дизайнер	Кырлан А.С.			04.11.26	Развёртка стены Г. Кабинет-гостевая (пом. 2)	Стадия: П; Лист: 86; Листов: 168

Развёртка стены А

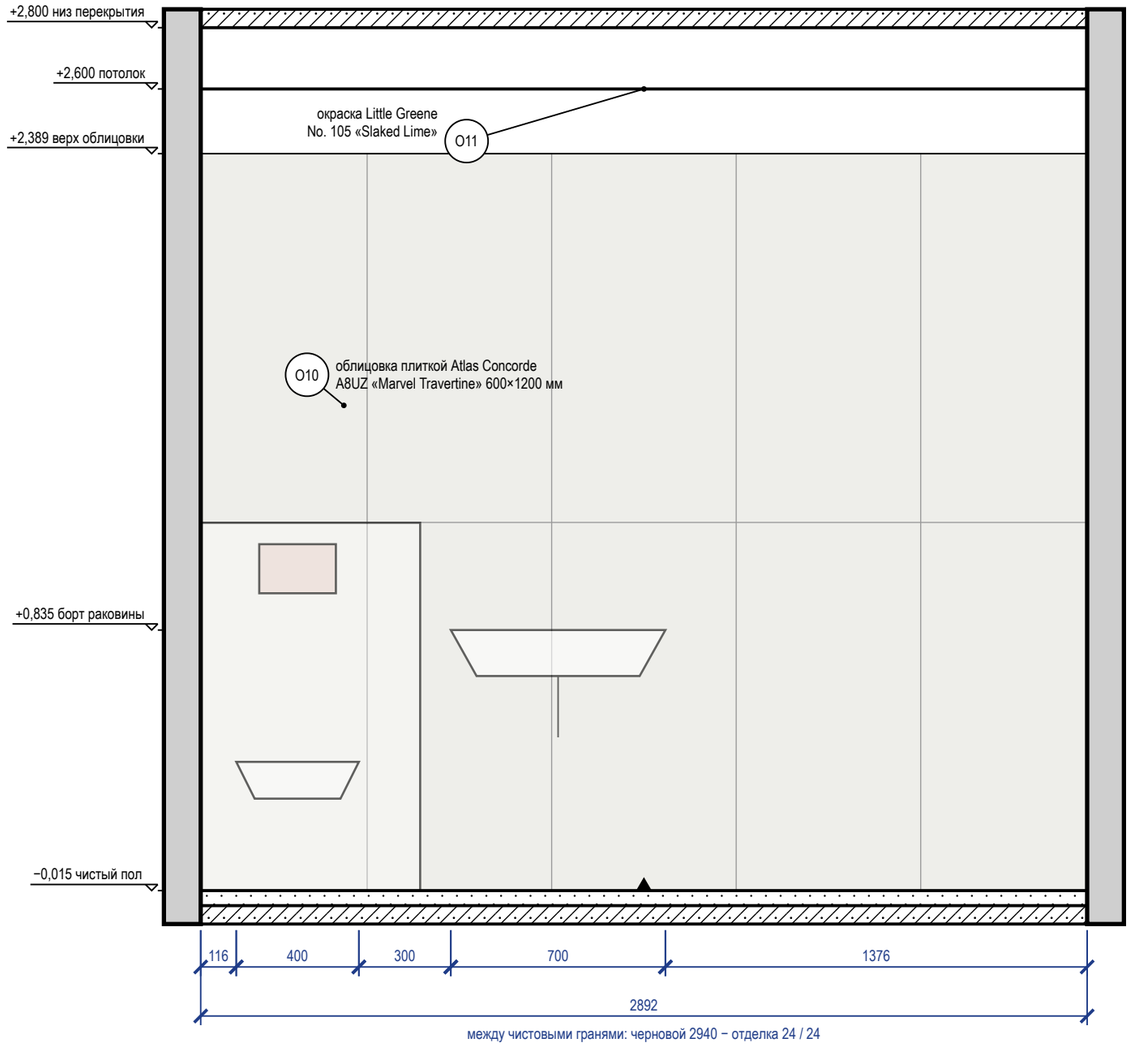

Развёртка стены Б


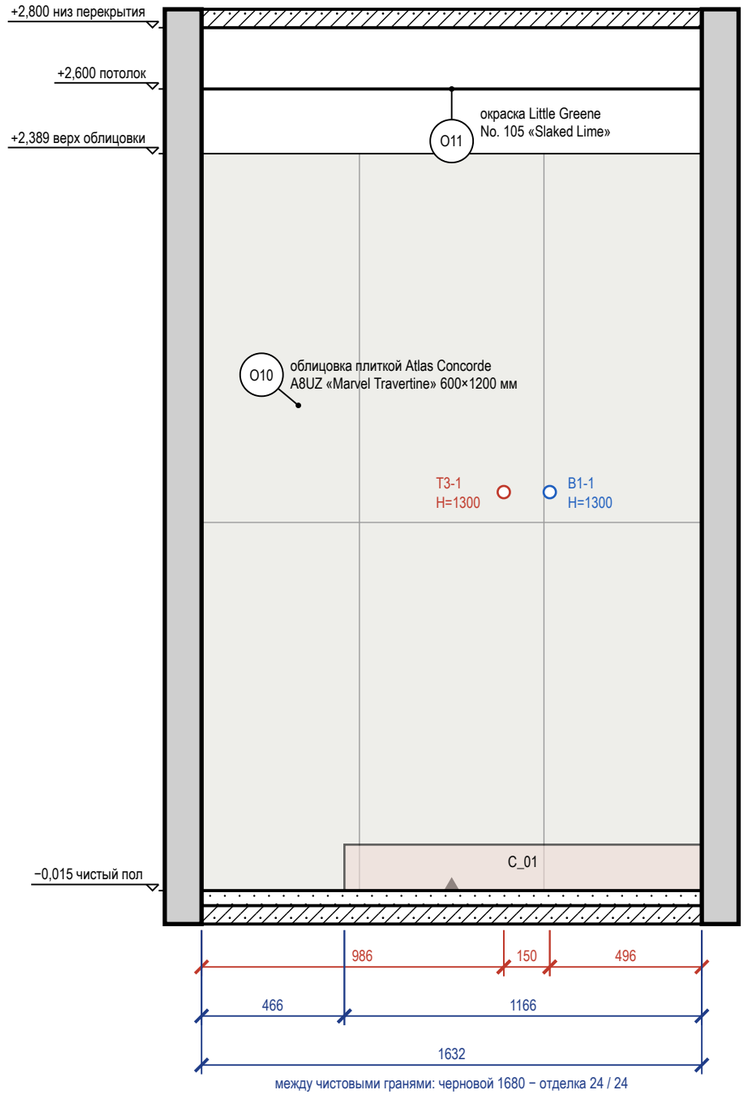


Схема развёрток (М 1:100)

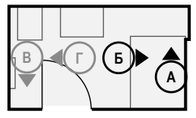

Ведомость отделки (на листе)

Марка	Поверхность	Материал, изделие	Цвет, код	Кол.
O10	стены	облицовка плиткой, Atlas Concorde Marvel Travertine, 600×1200×9 мм, A8UZ, затирка CG2WA	Atlas Concorde A8UZ «Marvel Travertine»	10,9 м²
O11	потолок	окраска, Little Greene Intelligent Bathroom, матовая, подготовка Q3	Little Greene No. 105 «Slaked Lime»	4,9 м²

Примечания

1. Размеры — в мм от чистовых поверхностей стен; условные обозначения и общие указания — лист 3.
2. Стена А показана двумя видами: здесь — архитектурная развёртка (мебель, отделка, проёмы, высоты), электроточки и выводы ВК с привязками и таблицей — на листе 88 («Привязки»).
3. Схема мебели, приборов и декора не является технической документацией для производства мебели; габариты — по паспортам изделий.
4. Выводы ВК — коды и высоты по листу выводов сантехники.
5. Облицовка — по сетке швов 2 мм, раскладка от оси стены (треугольник у пола), целые ряды от пола; подрезки — по листу раскладки плитки.
6. Гидроизоляция в 2 слоя, заход на стены 200 мм; у душа — на всю высоту стен душевой зоны и 500 мм за край душевой зоны — до облицовки, с актом скрытых работ и тестом проливом (узел — на листе узлов).

					Проект: Дом 331 м² — М 1:20
	Лист	№ док.	Подпись	Дата	Развёртки стен А, Б. Санузел 1 этажа (пом. 3)
Дизайнер	Кырлан А.С.			04.11.26	

Стадия	Лист	Листов
П	87	168

Развёртка стены А: электроточки и выводы

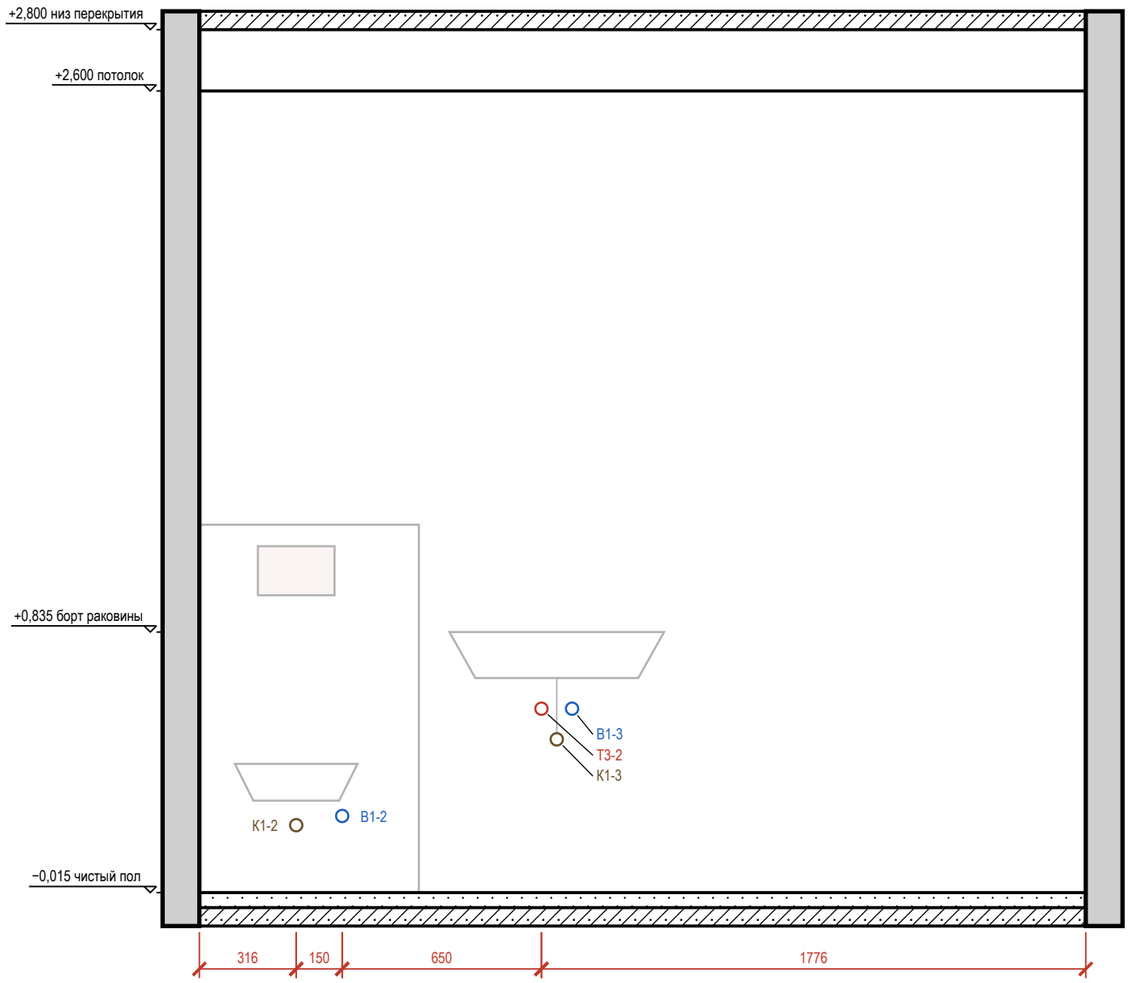



Таблица привязок электроточек и выводов

Марка	Назначение	От угла, мм	H от пола, мм	Примечание
К1-2	канализация — унитаз подвесной	316	220	Ø110
В1-2	холодная вода — унитаз подвесной	466	250	в раме инсталляции
Т3-2	горячая вода — умывальник	1116	600	межос. 100
К1-3	канализация — умывальник	1166	500	Ø50
В1-3	холодная вода — умывальник	1216	600	межос. 100

Условные обозначения

- вывод В1 (код — в ведомости привязок)
- вывод Т3 (код — в ведомости привязок)
- вывод К1 (код — в ведомости привязок)
- привязки точек и выводов от угла и от пола, мм
- марка развёртки: буква стены, стрелка — взгляд

Схема развёрток (М 1:50)

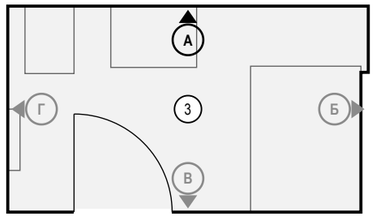


Примечания

1. Вид «Привязки» стены А — электроточки и выводы ВК; архитектурная развёртка (мебель, отделка, проёмы, высоты) — на листе 87. Мебель и приборы — подложкой для ориентира; их марки и обозначения мебели, проёмов и стен — там же.
2. Привязки — в мм: по горизонтали от левого чистового угла стены до оси изделия, H — от чистого пола до оси; все точки — в таблице привязок. Красная цепочка — привязки по осям; точки ближе 120 мм одна к другой в цепочку не дробятся — их привязки только в таблице.
3. Коды выводов ВК: В1 — холодная вода, Т3 — горячая вода, К1 — канализация; номер после дефиса — номер вывода на листе выводов сантехники.


					Проект: Дом 331 м²	М 1:20
	Лист	№ док.	Подпись	Дата	Привязки выводов ВК, стена А. Санузел 1 этажа (пом. 3)	Стадия / Лист / Листов
Дизайнер	Кырлан А.С.			04.11.26		П / 88 / 168

Развёртка стены В

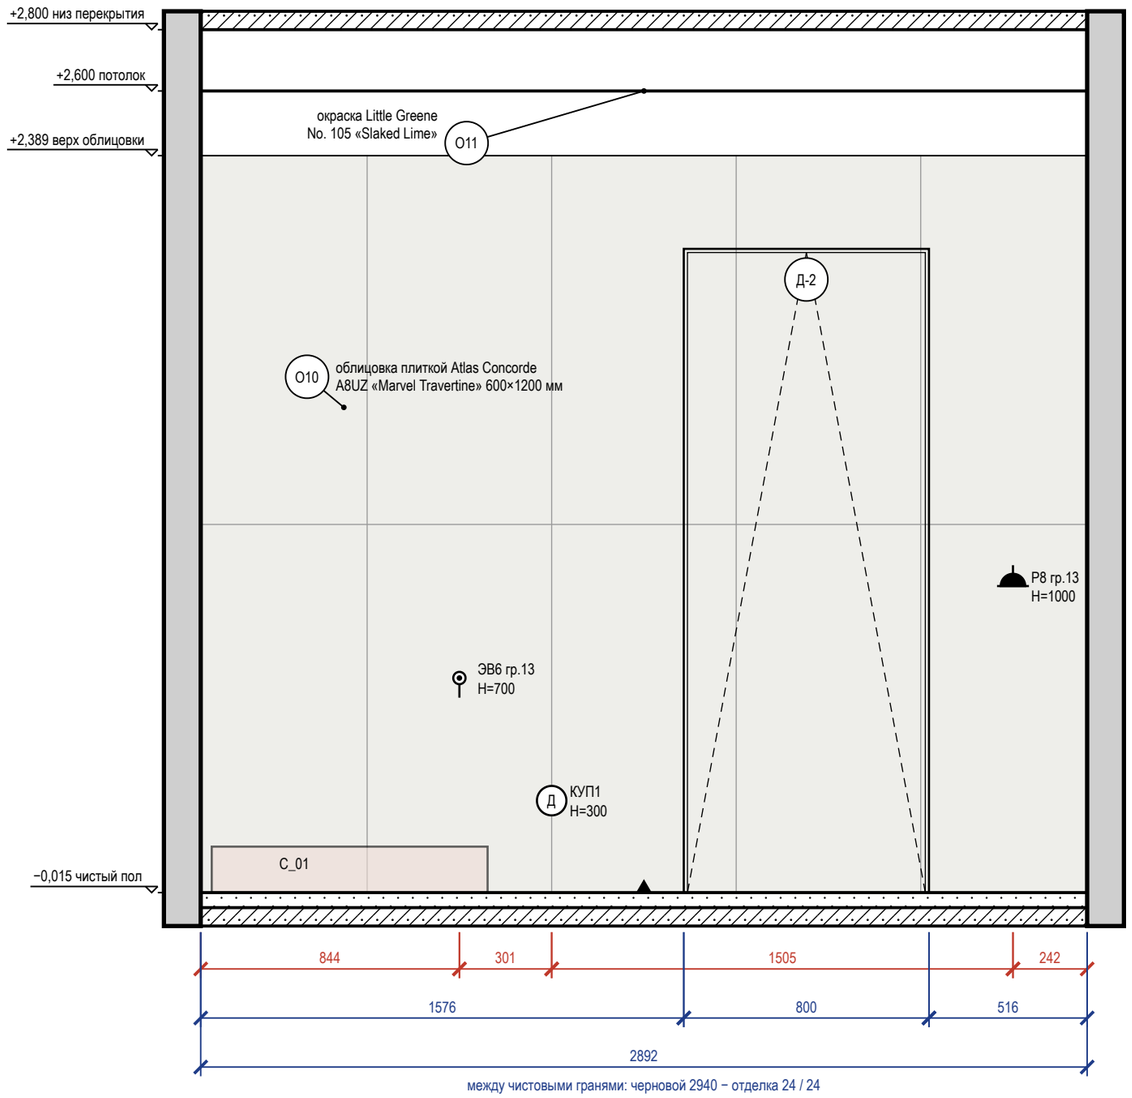


между чистовыми гранями: черновой 2940 − отделка 24 / 24

Развёртка стены Г

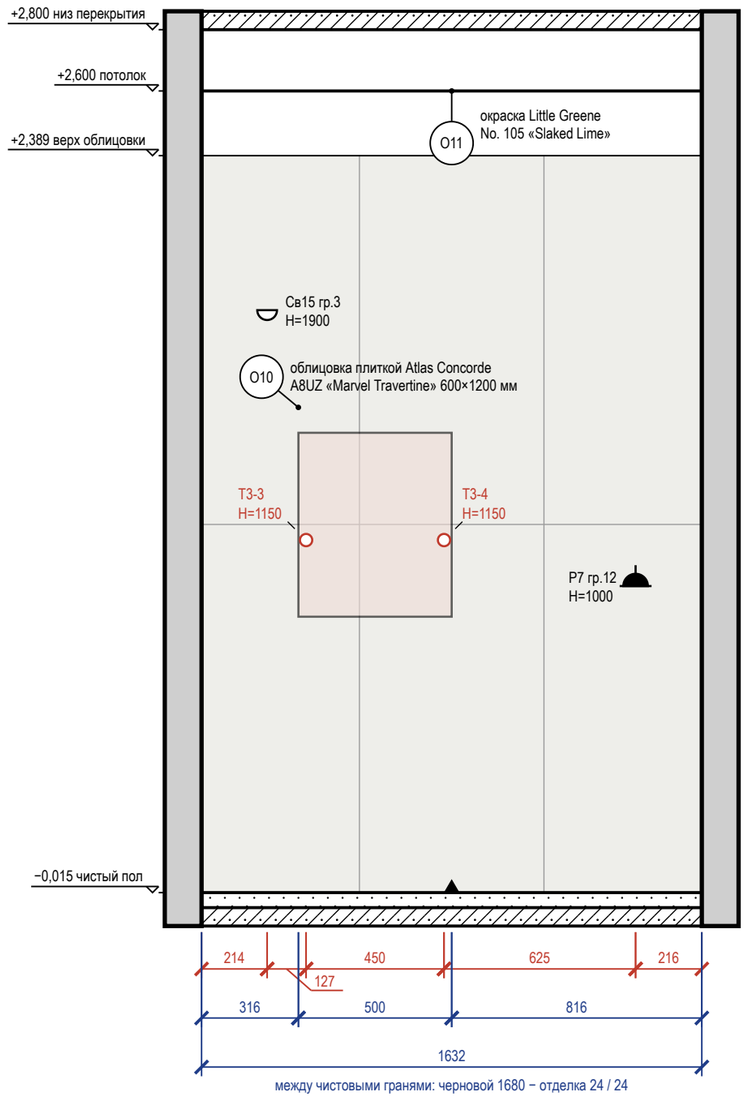

между чистовыми гранями: черновой 1680 − отделка 24 / 24

Схема развёрток (М 1:100)

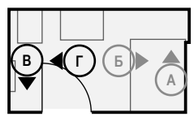

Ведомость отделки (на листе)

Марка	Поверхность	Материал, изделие	Цвет, код	Кол.
О10	стены	облицовка плиткой, Atlas Concorde Marvel Travertine, 600×1200×9 мм, A8UZ, затирка CG2WA	Atlas Concorde A8UZ «Marvel Travertine»	9,2 м²
О11	потолок	окраска, Little Greene Intelligent Bathroom, матовая, подготовка Q3	Little Greene No. 105 «Slaked Lime»	4,9 м²


Примечания

1. Размеры — в мм от чистовых поверхностей стен; условные обозначения и общие указания — лист 3.
2. Схема мебели, приборов и декора не является технической документацией для производства мебели; габариты — по паспортам изделий.
3. Выводы ВК — коды и высоты по листу выводов сантехники.
4. Облицовка — по сетке швов 2 мм, раскладка от оси стены (треугольник у пола), целые ряды от пола; подрезки — по листу раскладки плитки.
5. Гидроизоляция в 2 слоя, заход на стены 200 мм; у душа — на всю высоту стен душевой зоны и 500 мм за край душевой зоны — до облицовки, с актом скрытых работ и тестом проливом (узел — на листе узлов).
6. Двери скрытого монтажа — полотно в плоскости стены, отделка стены по полотну, плинтус прерывается у короба (узел — на листе узлов).

					Проект: Дом 331 м² — М 1:20
	Лист	№ док.	Подпись	Дата	
Дизайнер	Кырлан А.С.			04.11.26	Развёртки стен В, Г. Санузел 1 этажа (пом. 3)

Стадия	Лист	Листов
П	89	168

Развёртка стены А

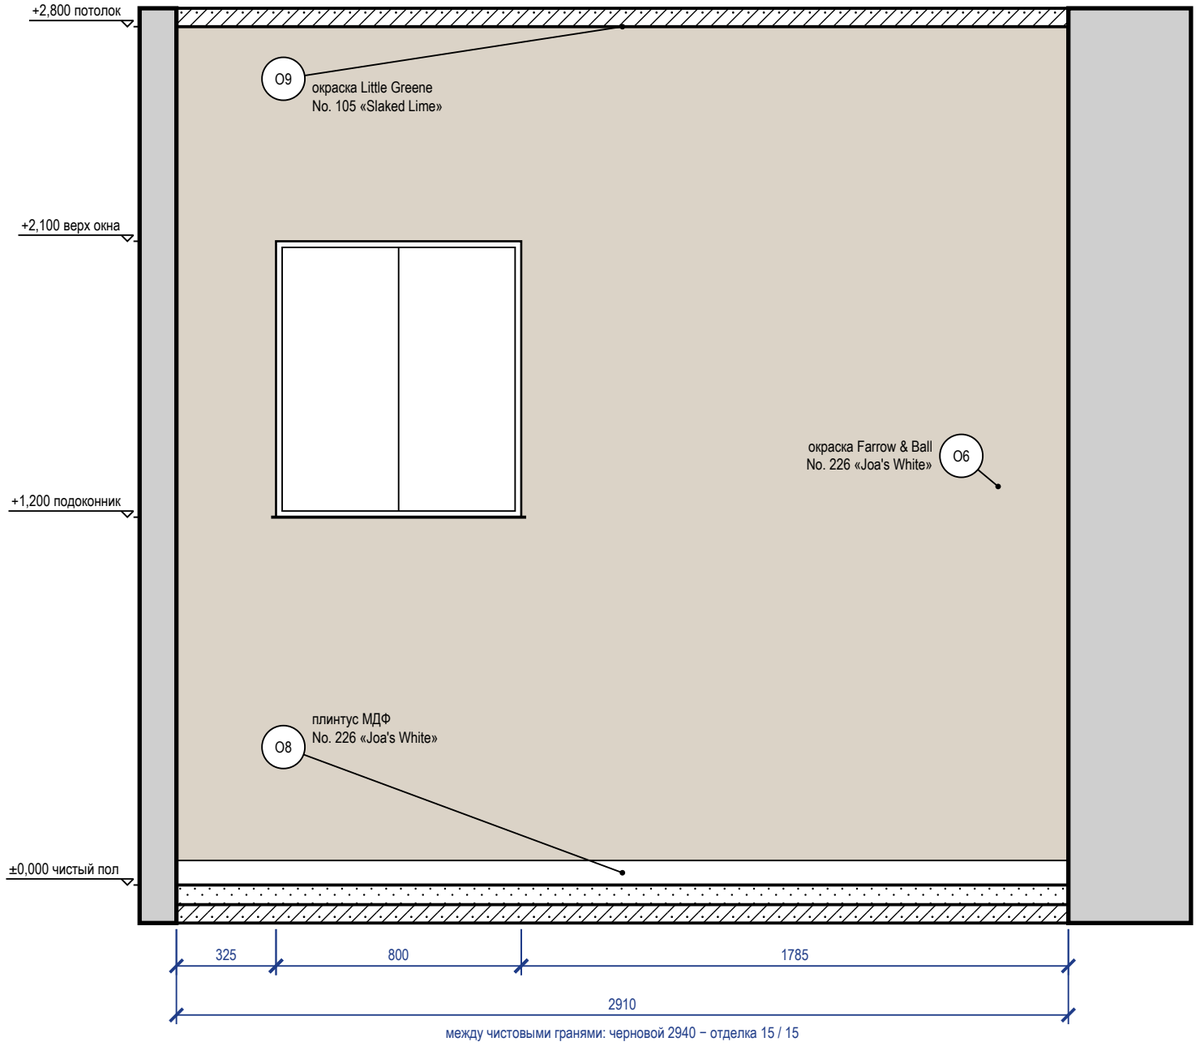

Развёртка стены Б


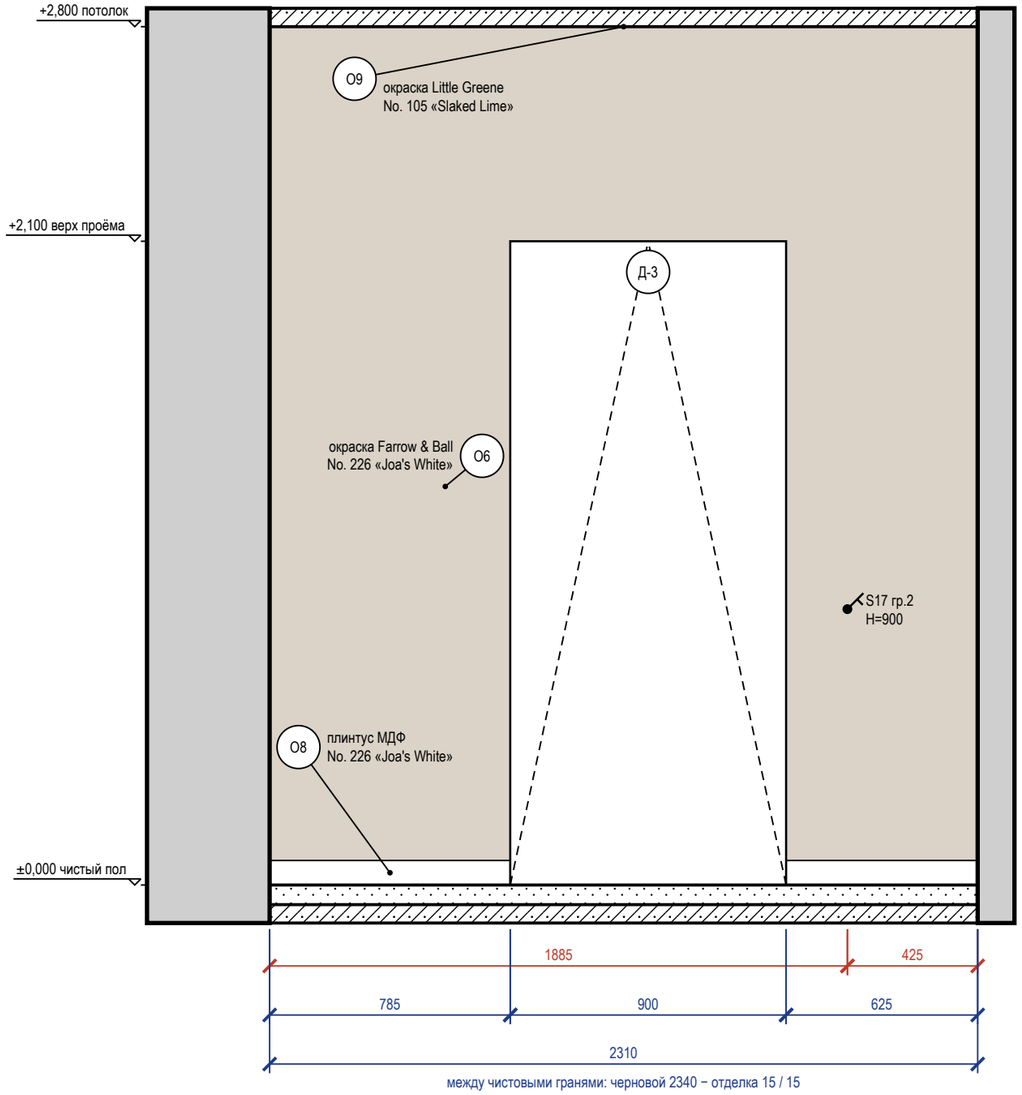


Схема развёрток (М 1:100)

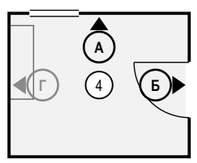

Ведомость отделки (на листе)

Марка	Поверхность	Материал, изделие	Цвет, код	Кол.
О6	стены	окраска, Farrow & Ball Modern Emulsion, матовая, подготовка Q3	Farrow & Ball No. 226 «Joa's White»	12 м²
О8	плинтус	плинтус МДФ, h 80 мм, аналог: плинтус МДФ под покраску 80×16	Farrow & Ball No. 226 «Joa's White»	4,3 м
О9	потолок	окраска, Little Greene Absolute Matt, глубокоматовая, подготовка Q3	Little Greene No. 105 «Slaked Lime»	6,9 м²

Примечания

1. Размеры — в мм от чистовых поверхностей стен; условные обозначения и общие указания — лист 3.

	Лист	№ док.	Подпись	Дата
Дизайнер	Кырлан А.С.			04.11.26

Проект: Дом 331 м² — **М 1:20**

Развёртки стен А, Б. Котельная (пом. 4)

Стадия	Лист	Листов
П	90	168

Развёртка стены Г


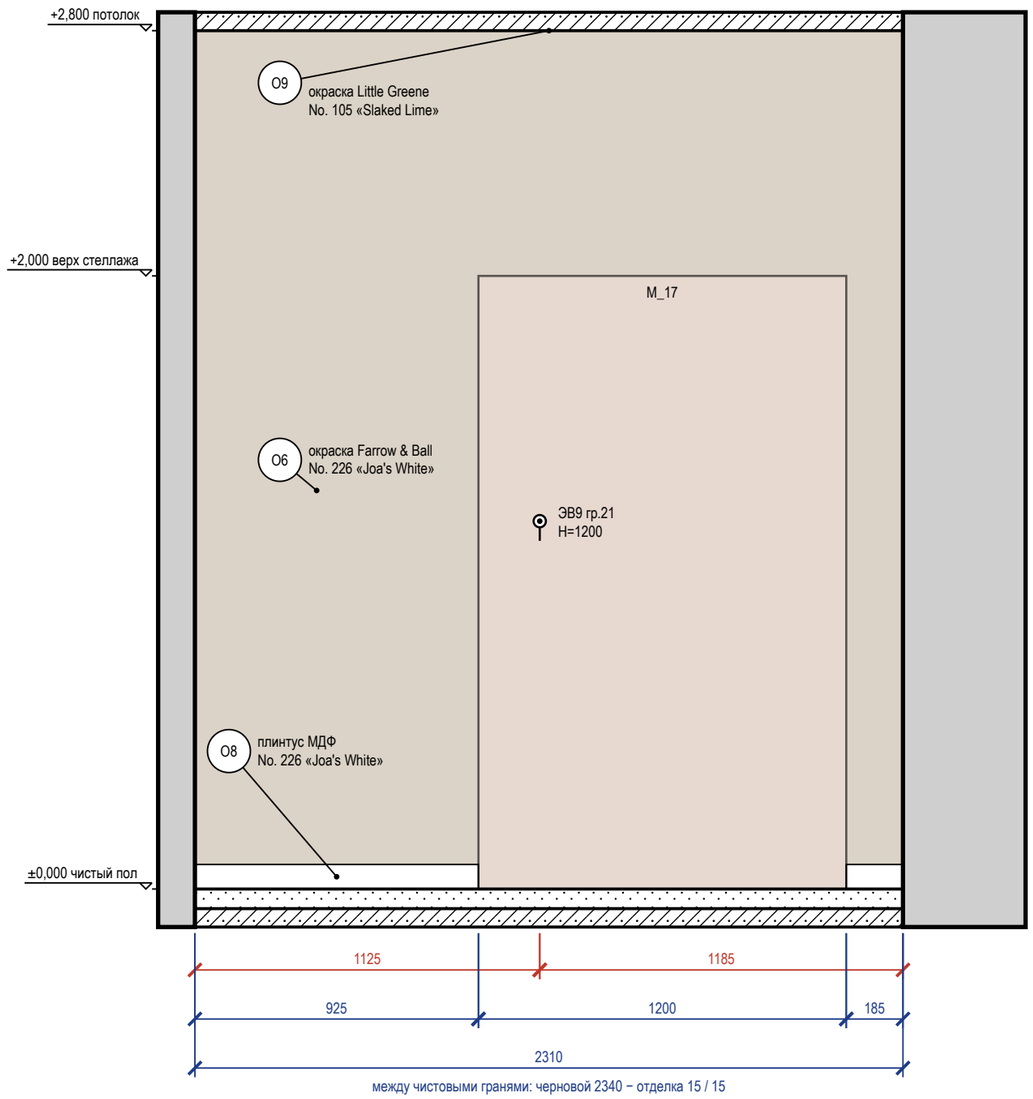


Схема развёрток (М 1:100)

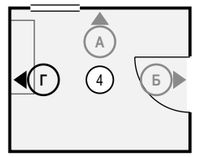

Ведомость отделки (на листе)

Марка	Поверхность	Материал, изделие	Цвет, код	Кол.
О6	стены	окраска, Farrow & Ball Modern Emulsion, матовая, подготовка Q3	Farrow & Ball No. 226 «Joa's White»	6,5 м²
О8	плинтус	плинтус МДФ, h 80 мм, аналог: плинтус МДФ под покраску 80×16	Farrow & Ball No. 226 «Joa's White»	1,1 м
О9	потолок	окраска, Little Greene Absolute Matt, глубокоматовая, подготовка Q3	Little Greene No. 105 «Slaked Lime»	6,9 м²

Примечания

1. Размеры — в мм от чистовых поверхностей стен; условные обозначения и общие указания — лист 3.

					Проект: Дом 331 м²	М 1:20
	Лист	№ док.	Подпись	Дата		
Дизайнер	Кырлан А.С.			04.11.26	Развёртка стены Г. Котельная (пом. 4)	Стадия: П; Лист: 91; Листов: 168

Развёртка стены А


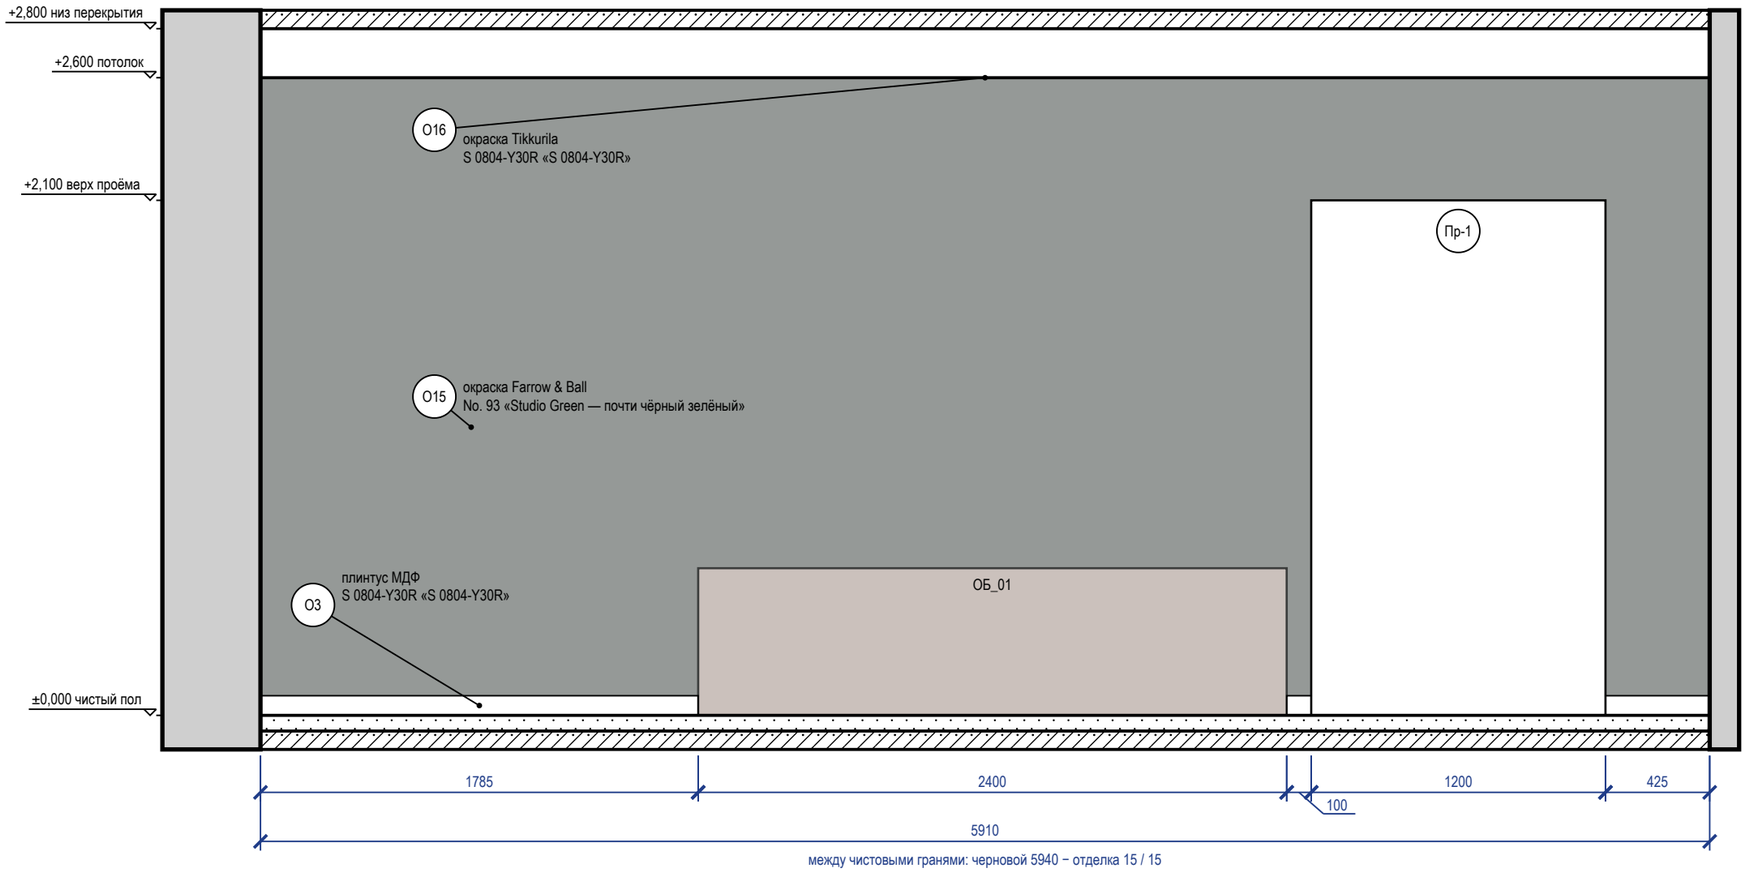


Схема развёрток (М 1:100)

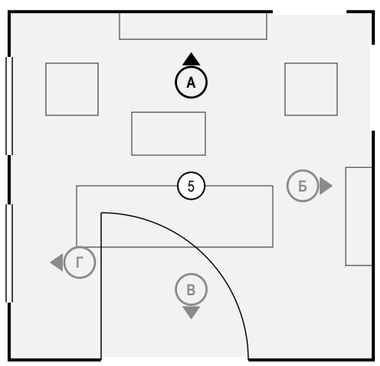

Ведомость отделки (на листе)

Марка	Поверхность	Материал, изделие	Цвет, код	Кол.
О3	плинтус	плинтус МДФ, h 80 мм, аналог: плинтус МДФ под окраску 80×16 мм, полуглянцевая	NCS S 0804-Y30R «S 0804-Y30R»	2,3 м
О15	акцентная стена	окраска, Farrow & Ball Modern Emulsion, аналог: интерьерная краска, класс 2 по EN 13300, глубокоматовая/матовая, база C, матовая, подготовка К3	Farrow & Ball No. 93 «Studio Green — почти чёрный зелёный»	12,8 м²
О16	потолок	окраска, Tikkurila Anti-Reflex 2, глубокоматовая, подготовка Q3	NCS S 0804-Y30R «S 0804-Y30R»	33,7 м²

Примечания

1. Размеры — в мм от чистовых поверхностей стен; условные обозначения и общие указания — лист 3.
2. Стена А показана двумя видами: здесь — архитектурная развёртка (мебель, отделка, проёмы, высоты), электроточки и выводы ВК с привязками и таблицей — на листе 93 («Привязки»).
3. Потолок — у каждой стены свой, по плану потолков (ПТ2); ступени — зоной, кромка короба перед нишей — тонкой линией; в поле потолка: ПТ3 +2,700.

					Проект: Дом 331 м²	М 1:25
	Лист	№ док.	Подпись	Дата		
Дизайнер	Кырлан А.С.			04.11.26	Развёртка стены А. Гостиная (пом. 5)	Стадия: П; Лист: 92; Листов: 168

Развёртка стены А: электроточки и выводы

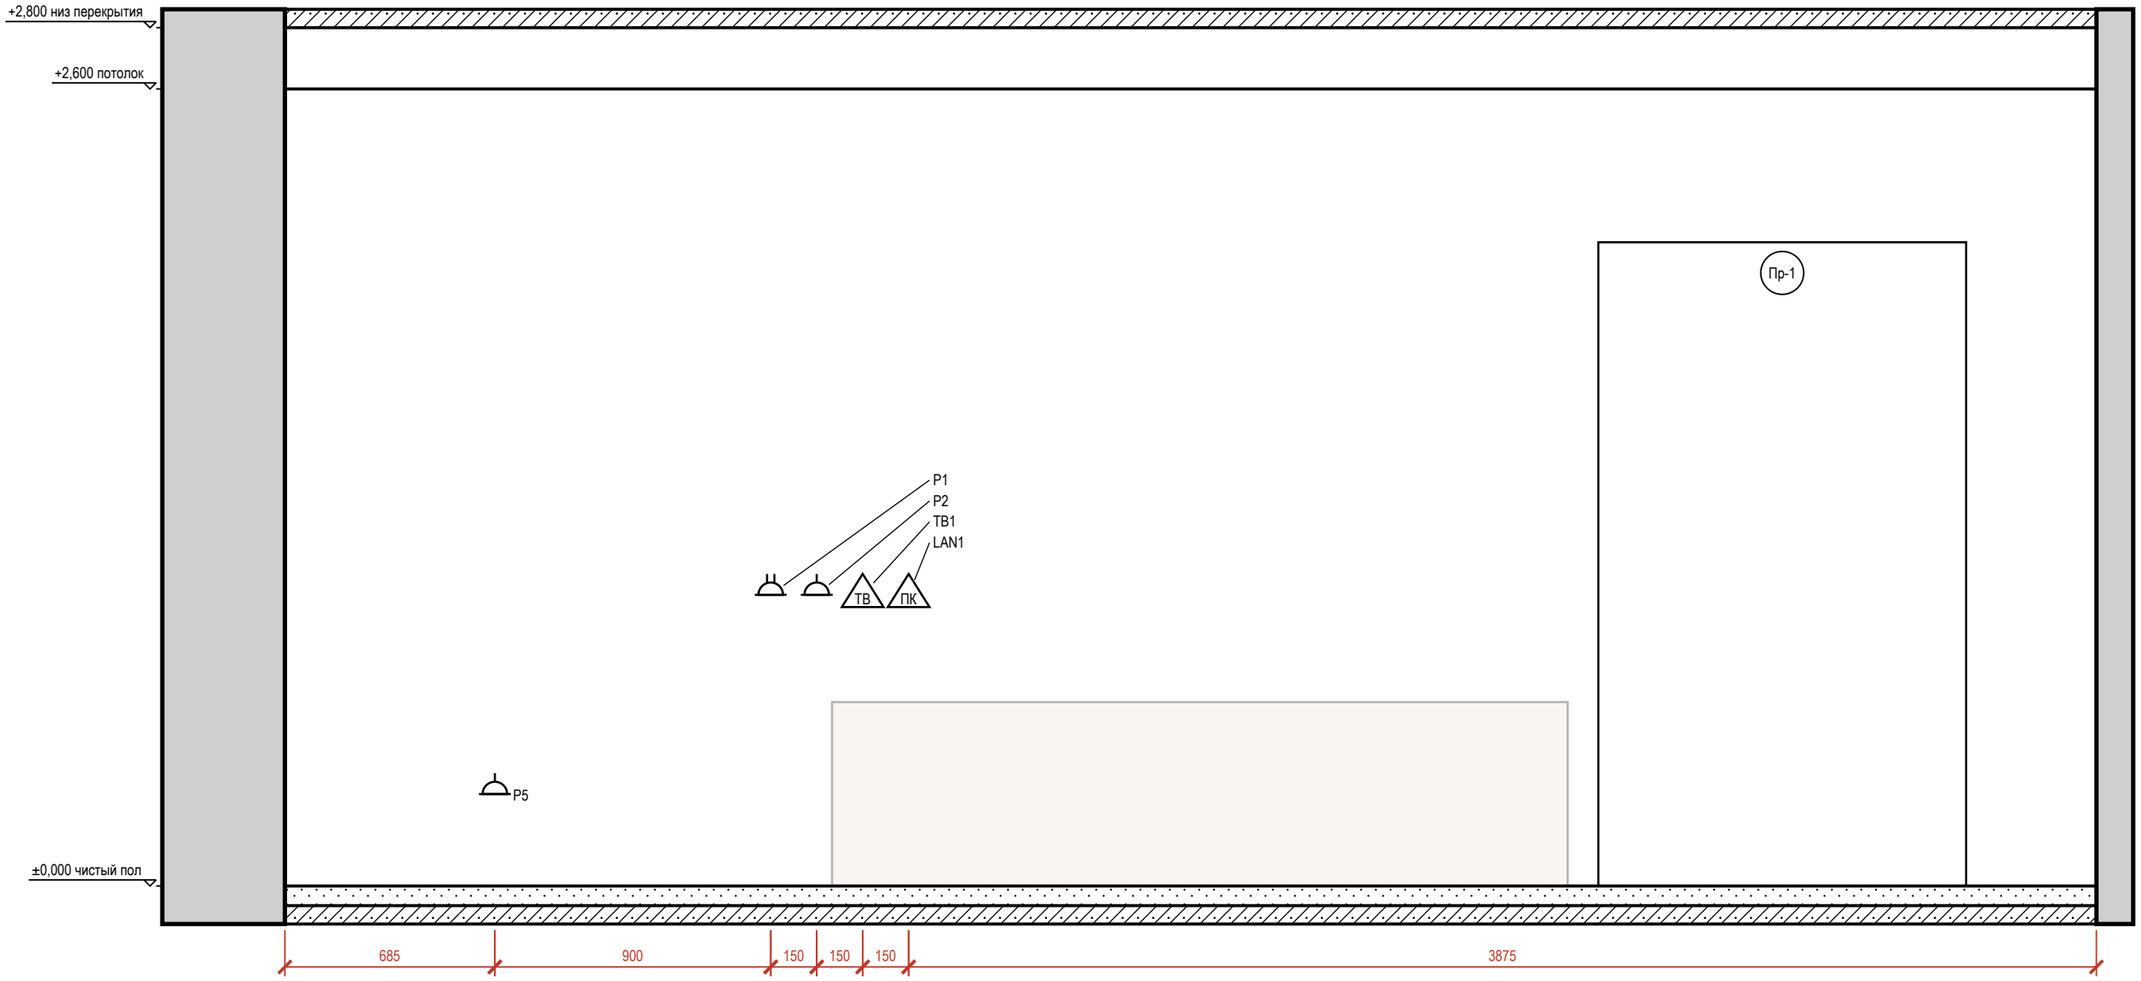



Таблица привязок электроточек и выводов

Марка	Назначение	От угла, мм	Н от пола, мм	Примечание
P5	розетка: общего назначения	685	300	гр. 5
P1	розетка: ТВ-зона: телевизор, медиаплеер	1585	950	рамка 2 поста, гр. 5
P2	розетка: ТВ-зона: саундбар	1735	950	гр. 5
TB1	розетка ТВ: ТВ-зона	1885	950	
LAN1	розетка RJ45: ТВ-зона	2035	950	

Условные обозначения

- розетка с заземляющим контактом; у знака — марка, ×N постов в рамке, гр. — группа щита, Н — высота оси, мм
- ПК — розетка компьютерная RJ45
- ТВ — розетка телевизионная
- привязки точек и выводов от угла и от пола, мм
- A — марка развёртки: буква стены, стрелка — взгляд

Схема развёрток (М 1:200)

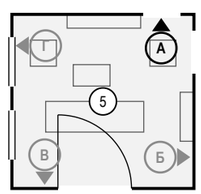

Примечания

1. Вид «Привязки» стены А — электроточки и выводы ВК; архитектурная развёртка (мебель, отделка, проёмы, высоты) — на листе 92. Мебель и приборы — подложкой для ориентира; их марки и обозначения мебели, проёмов и стен — там же.
2. Привязки — в мм: по горизонтали от левого чистового угла стены до оси изделия, Н — от чистого пола до оси; все точки — в таблице привязок. Красная цепочка — привязки по осям; точки ближе 120 мм одна к другой в цепочку не дробятся — их привязки только в таблице.
3. У знака — марка электроточки (Р — розетка, S — выключатель, Св — светильник, ЭВ — вывод кабеля); условные обозначения и общие указания — лист 3.

	Лист	№ док.	Подпись	Дата
Дизайнер	Кырлан А.С.			04.11.26

Проект: Дом 331 м² — М 1:20

Привязки электроточек, стена А. Гостиная (пом. 5)

Стадия	Лист	Листов
П	93	168

Развёртка стены Б


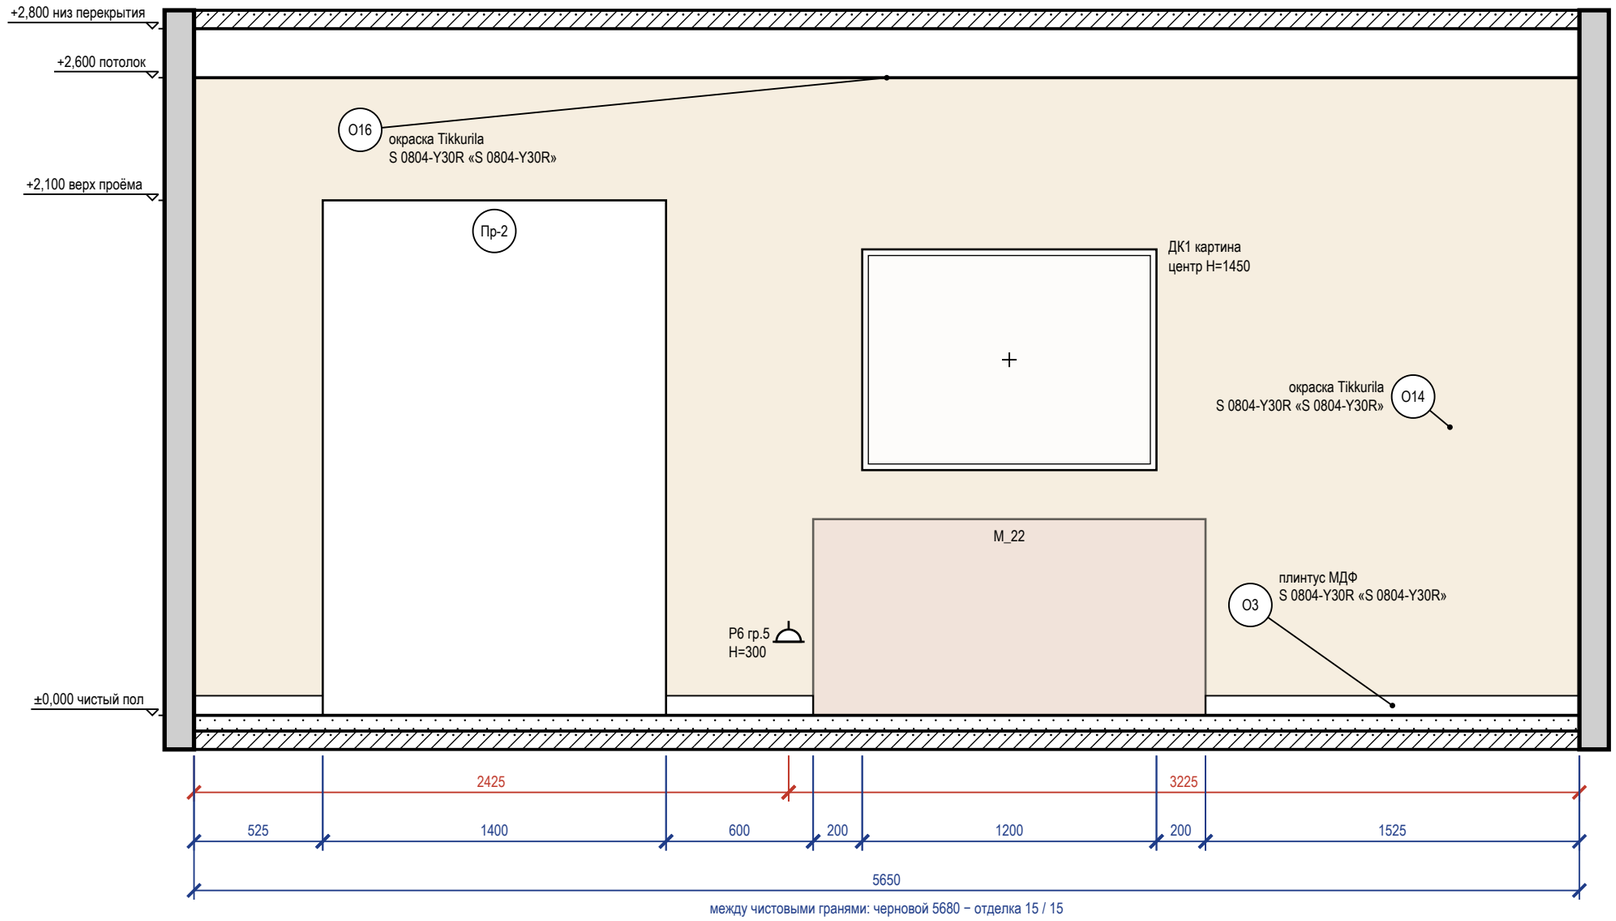


Схема развёрток (М 1:100)

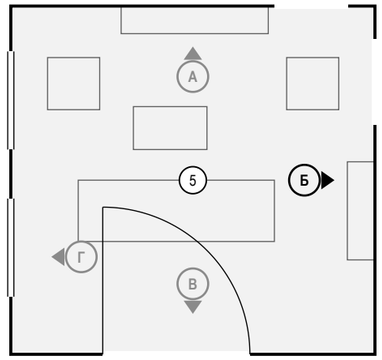

Ведомость отделки (на листе)

Марка	Поверхность	Материал, изделие	Цвет, код	Кол.
О3	плинтус	плинтус МДФ, h 80 мм, аналог: плинтус МДФ под окраску 80×16 мм, полуглянцевая	NCS S 0804-Y30R «S 0804-Y30R»	2,6 м
О14	стены	окраска, Tikkurila Optiva 5 Matt, матовая, подготовка К3	NCS S 0804-Y30R «S 0804-Y30R»	11,8 м²
О16	потолок	окраска, Tikkurila Anti-Reflex 2, глубокоматовая, подготовка Q3	NCS S 0804-Y30R «S 0804-Y30R»	33,7 м²

Примечания

1. Размеры — в мм от чистовых поверхностей стен; условные обозначения и общие указания — лист 3.
2. Картины и зеркала крепить к основанию по паспорту изделия (закладные и анкеры — в перечне скрытых работ); крест — ось центра предмета.
3. Потолок — у каждой стены свой, по плану потолков (ПТ2); ступени — зоной, кромка короба перед нишей — тонкой линией; в поле потолка: ПТ3 +2,700.

	Лист	№ док.	Подпись	Дата
Дизайнер	Кырлан А.С.			04.11.26

Проект: Дом 331 м² — **М 1:25**

Развёртка стены Б. Гостиная (пом. 5)

Стадия	Лист	Листов
П	94	168

выпуск 04.11.2026 № f163a372b2 · стр. 94 из 168

Развёртка стены В


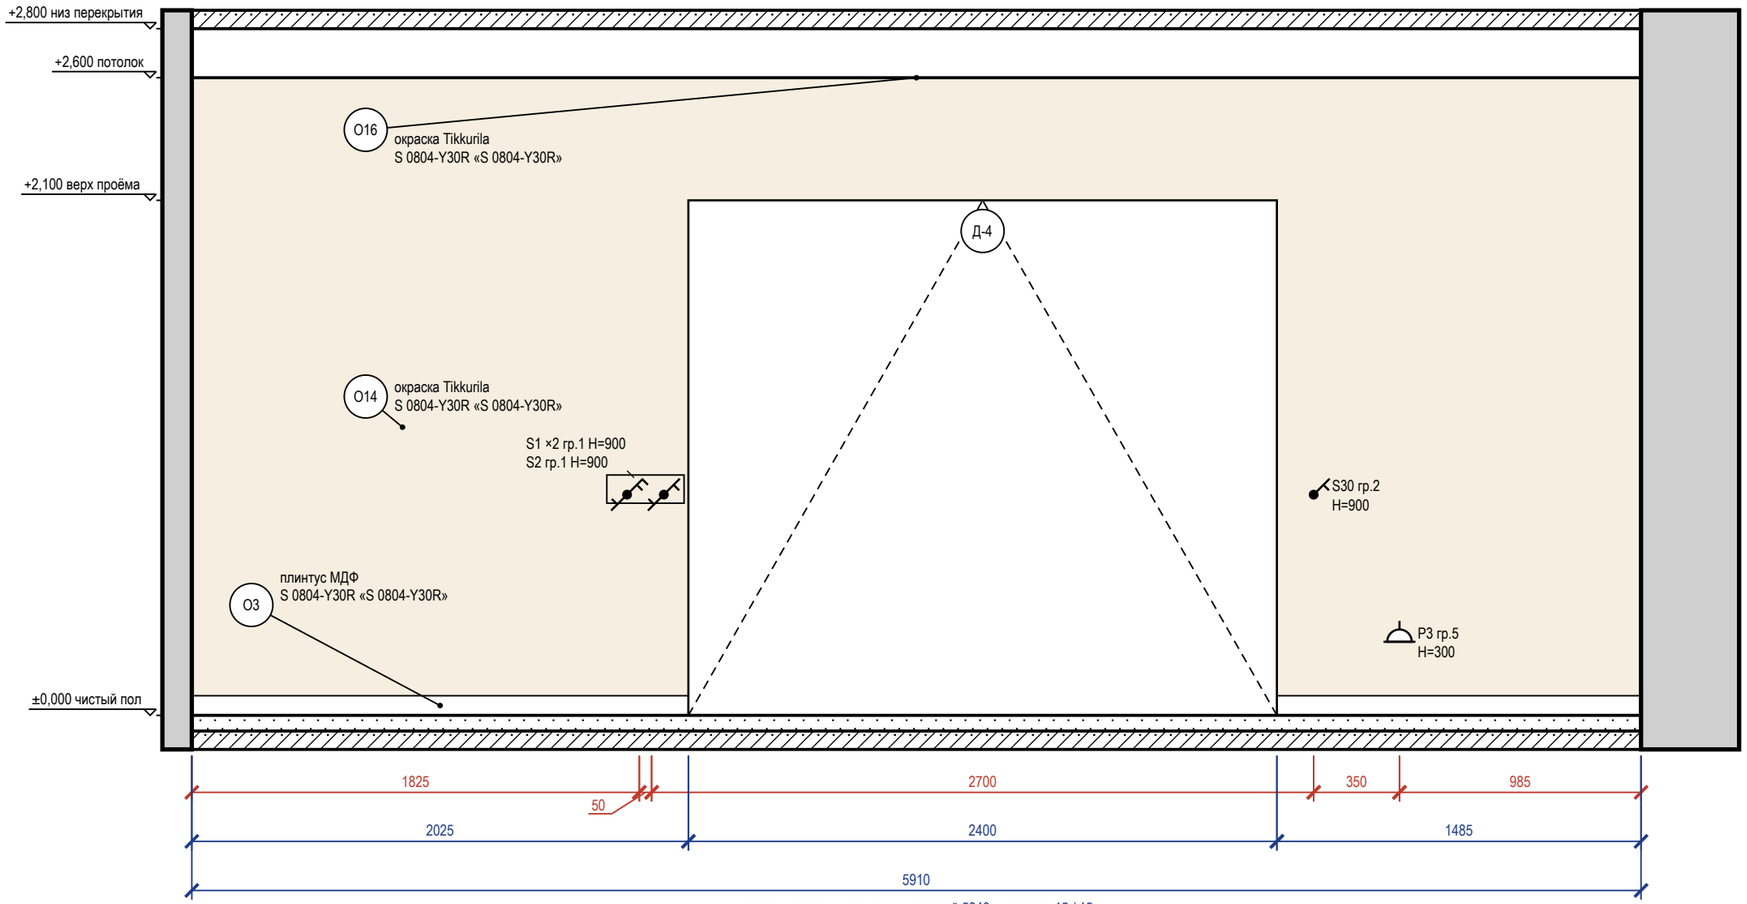


Схема развёрток (М 1:100)

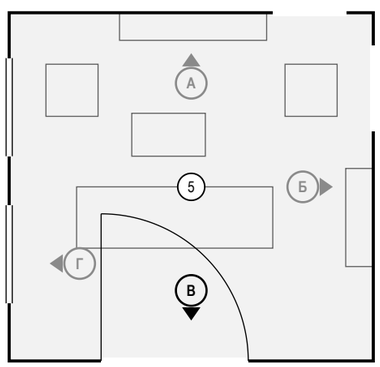

Ведомость отделки (на листе)

Марка	Поверхность	Материал, изделие	Цвет, код	Кол.
О3	плинтус	плинтус МДФ, h 80 мм, аналог: плинтус МДФ под окраску 80×16 мм, полуглянцевая	NCS S 0804-Y30R «S 0804-Y30R»	3,5 м
О14	стены	окраска, Tikkurila Optiva 5 Matt, матовая, подготовка К3	NCS S 0804-Y30R «S 0804-Y30R»	10,3 м²
О16	потолок	окраска, Tikkurila Anti-Reflex 2, глубокоматовая, подготовка Q3	NCS S 0804-Y30R «S 0804-Y30R»	33,7 м²

Примечания

1. Размеры — в мм от чистовых поверхностей стен; условные обозначения и общие указания — лист 3.
2. Потолок — у каждой стены свой, по плану потолков (ПТ2); ступени — зоной, кромка короба перед нишей — тонкой линией; в поле потолка: ПТ3 +2,700.

					Проект: Дом 331 м² — М 1:25
	Лист	№ док.	Подпись	Дата	Развёртка стены В. Гостиная (пом. 5)
Дизайнер	Кырлан А.С.			04.11.26	Стадия: П; Лист: 95; Листов: 168

Развёртка стены Г


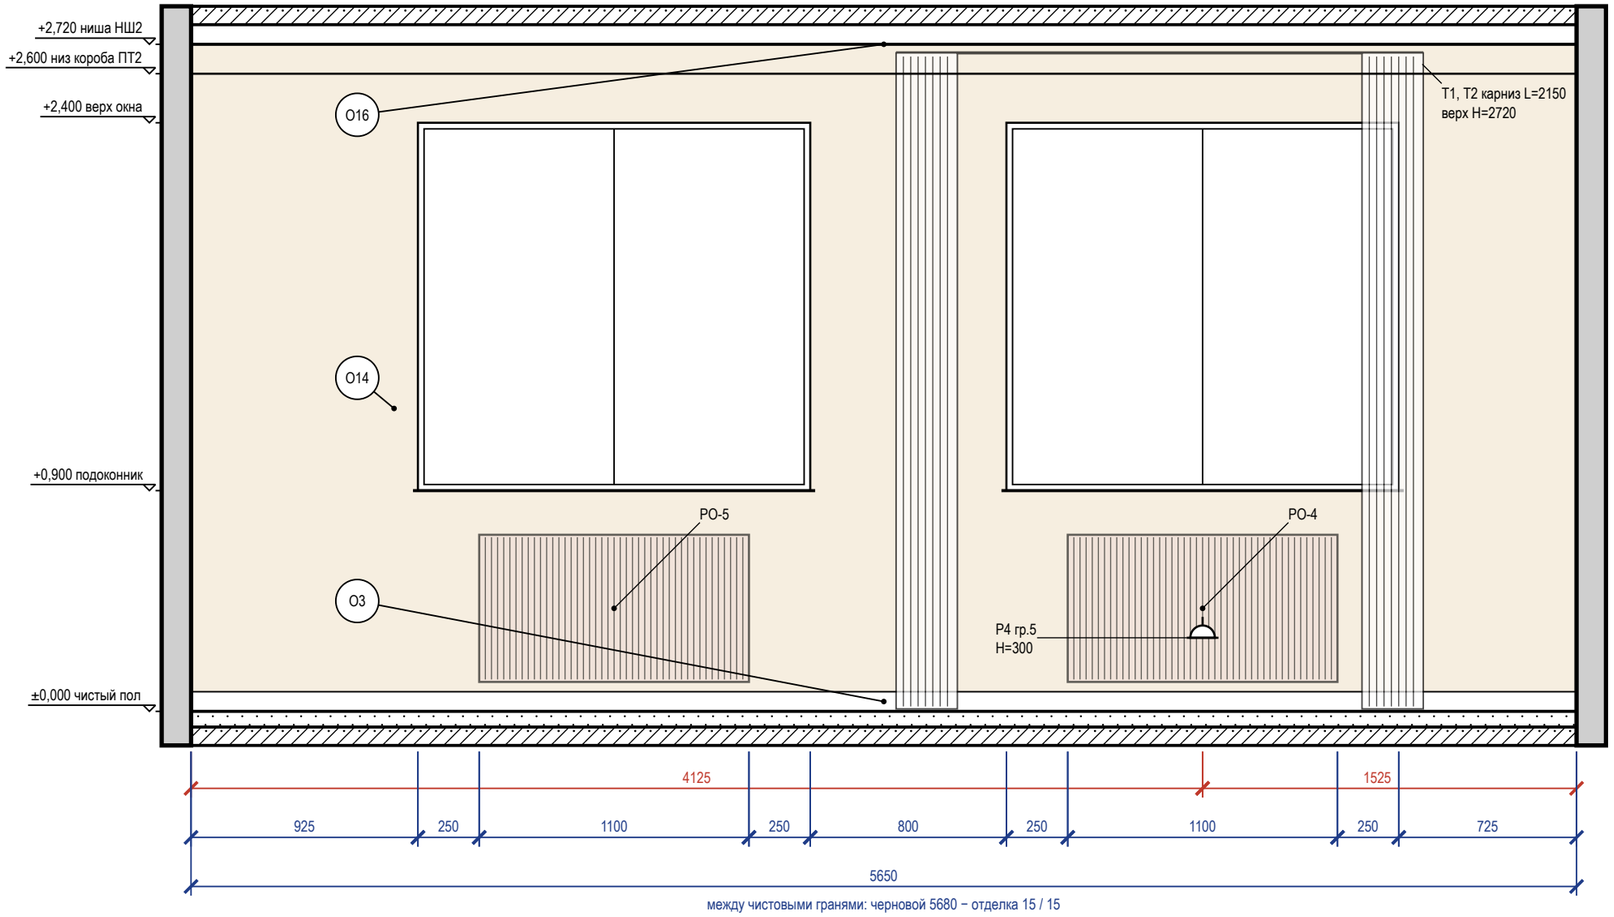


Схема развёрток (М 1:100)

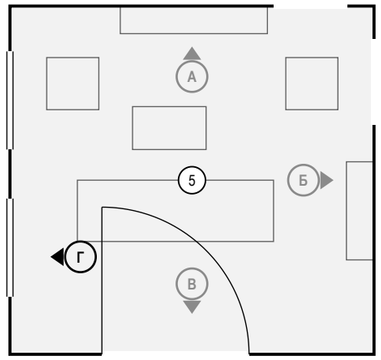

Ведомость отделки (на листе)

Марка	Поверхность	Материал, изделие	Цвет, код	Кол.
О3	плинтус	плинтус МДФ, h 80 мм, аналог: плинтус МДФ под окраску 80×16 мм, полуглянцевая	NCS S 0804-Y30R «S 0804-Y30R»	5,7 м
О14	стены	окраска, Tikkurila Optiva 5 Matt, матовая, подготовка К3	NCS S 0804-Y30R «S 0804-Y30R»	10,6 м²
О16	потолок	окраска, Tikkurila Anti-Reflex 2, глубокоматовая, подготовка Q3	NCS S 0804-Y30R «S 0804-Y30R»	33,7 м²

Примечания

1. Размеры — в мм от чистовых поверхностей стен; условные обозначения и общие указания — лист 3.
2. Карнизы (шины) — по ведомости текстиля декоратора: длина L и верх H на развёртке — те же числа, что в ведомости; крепление — до окраски потолка.
3. Потолок — у каждой стены свой, по плану потолков (НШ2, ПТ2); ступени — зоной, кромка короба перед нишей — тонкой линией; в поле потолка: ПТ3 +2,700.

	Лист	№ док.	Подпись	Дата
Дизайнер	Кырлан А.С.			04.11.26

Проект: Дом 331 м² — **М 1:25**

Развёртка стены Г. Гостиная (пом. 5)

Стадия	Лист	Листов
П	96	168

Развёртка стены А


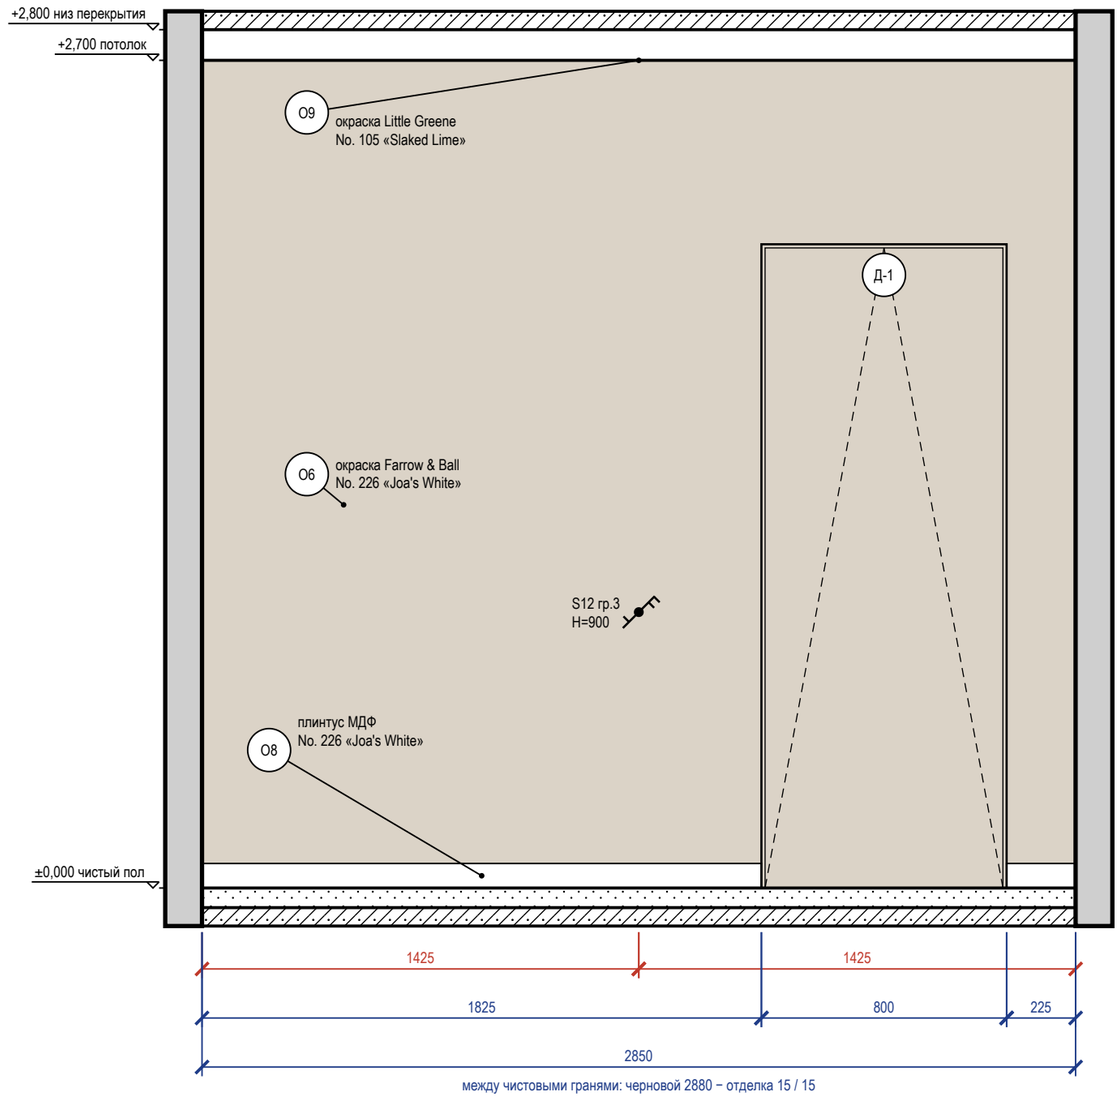


Схема развёрток (М 1:100)

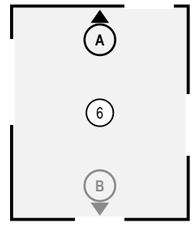


Ведомость отделки (на листе)

Марка	Поверхность	Материал, изделие	Цвет, код	Кол.
О6	стены	окраска, Farrow & Ball Modern Emulsion, матовая, подготовка Q3	Farrow & Ball No. 226 «Joa's White»	6 м²
О8	плинтус	плинтус МДФ, h 80 мм, аналог: плинтус МДФ под покраску 80×16	Farrow & Ball No. 226 «Joa's White»	2 м
О9	потолок	окраска, Little Greene Absolute Matt, глубокоматовая, подготовка Q3	Little Greene No. 105 «Slaked Lime»	10 м²

3 **Дверь скрытого монтажа в плоскости стены, плинтус (М 1:10)**

Узел 3 — лист С9

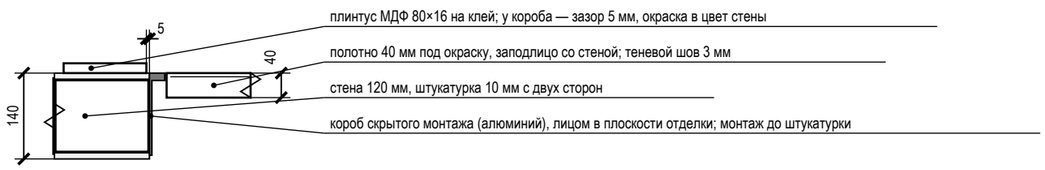

Примечания

1. Размеры — в мм от чистовых поверхностей стен; условные обозначения и общие указания — лист 3.
2. Двери скрытого монтажа — полотно в плоскости стены, отделка стены по полотну, плинтус прерывается у короба (узел — на листе узлов).

					Проект: Дом 331 м²	М 1:20
	Лист	№ док.	Подпись	Дата		
Дизайнер	Кырлан А.С.			04.11.26	Развёртка стены А. Холл с лестницей (пом. 6)	Стадия: П; Лист: 97; Листов: 168

Развёртка стены В


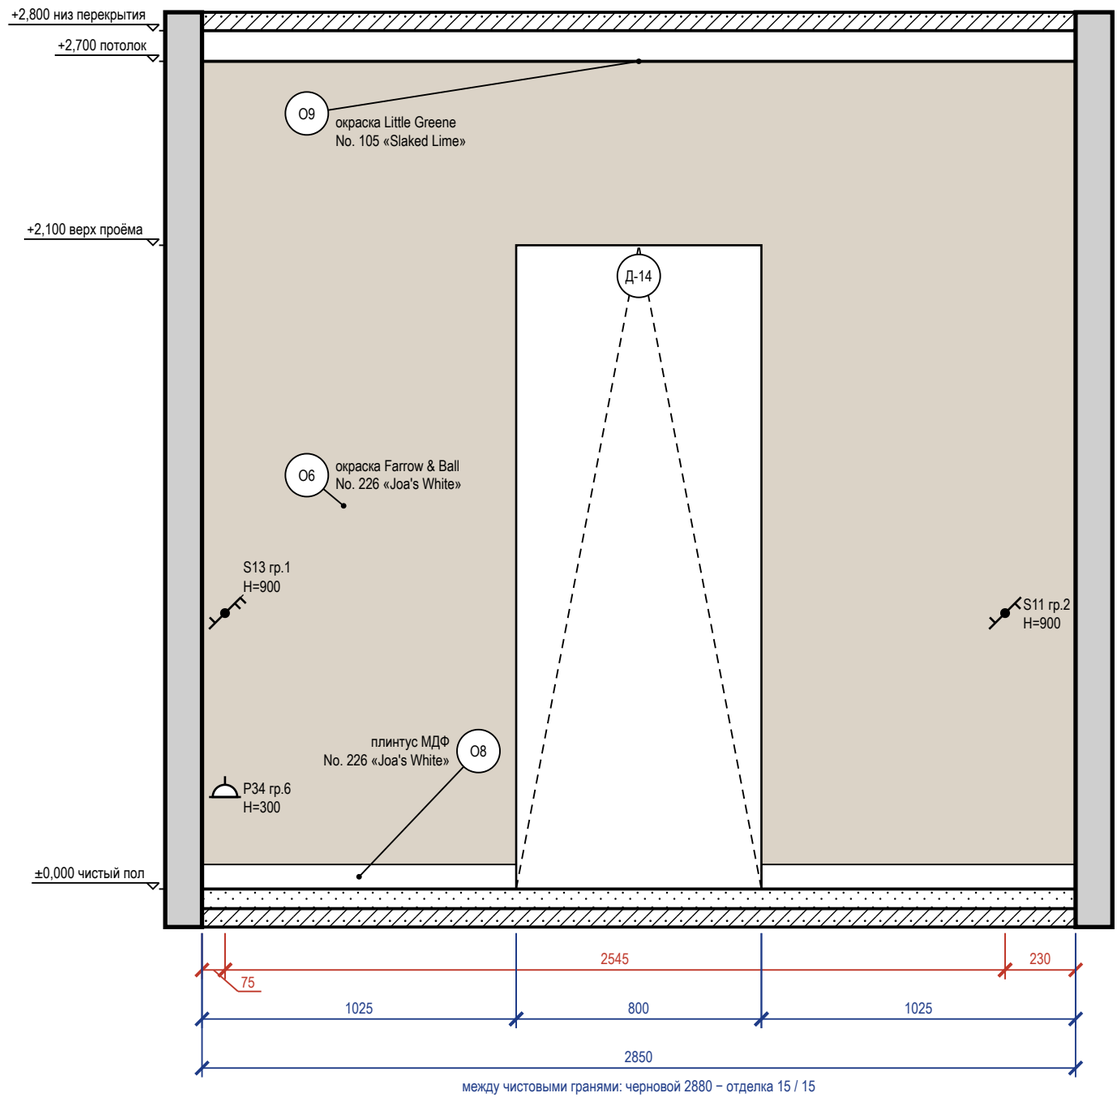


Схема развёрток (М 1:100)

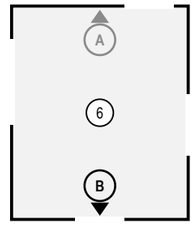

Ведомость отделки (на листе)

Марка	Поверхность	Материал, изделие	Цвет, код	Кол.
О6	стены	окраска, Farrow & Ball Modern Emulsion, матовая, подготовка Q3	Farrow & Ball No. 226 «Joa's White»	6 м²
О8	плинтус	плинтус МДФ, h 80 мм, аналог: плинтус МДФ под покраску 80×16	Farrow & Ball No. 226 «Joa's White»	2 м
О9	потолок	окраска, Little Greene Absolute Matt, глубокоматовая, подготовка Q3	Little Greene No. 105 «Slaked Lime»	10 м²

Примечания

1. Размеры — в мм от чистовых поверхностей стен; условные обозначения и общие указания — лист 3.

					Проект: Дом 331 м²	М 1:20
	Лист	№ док.	Подпись	Дата		
Дизайнер	Кырлан А.С.			04.11.26	Развёртка стены В. Холл с лестницей (пом. 6)	Стадия: П; Лист: 98; Листов: 168

Развёртка стены В


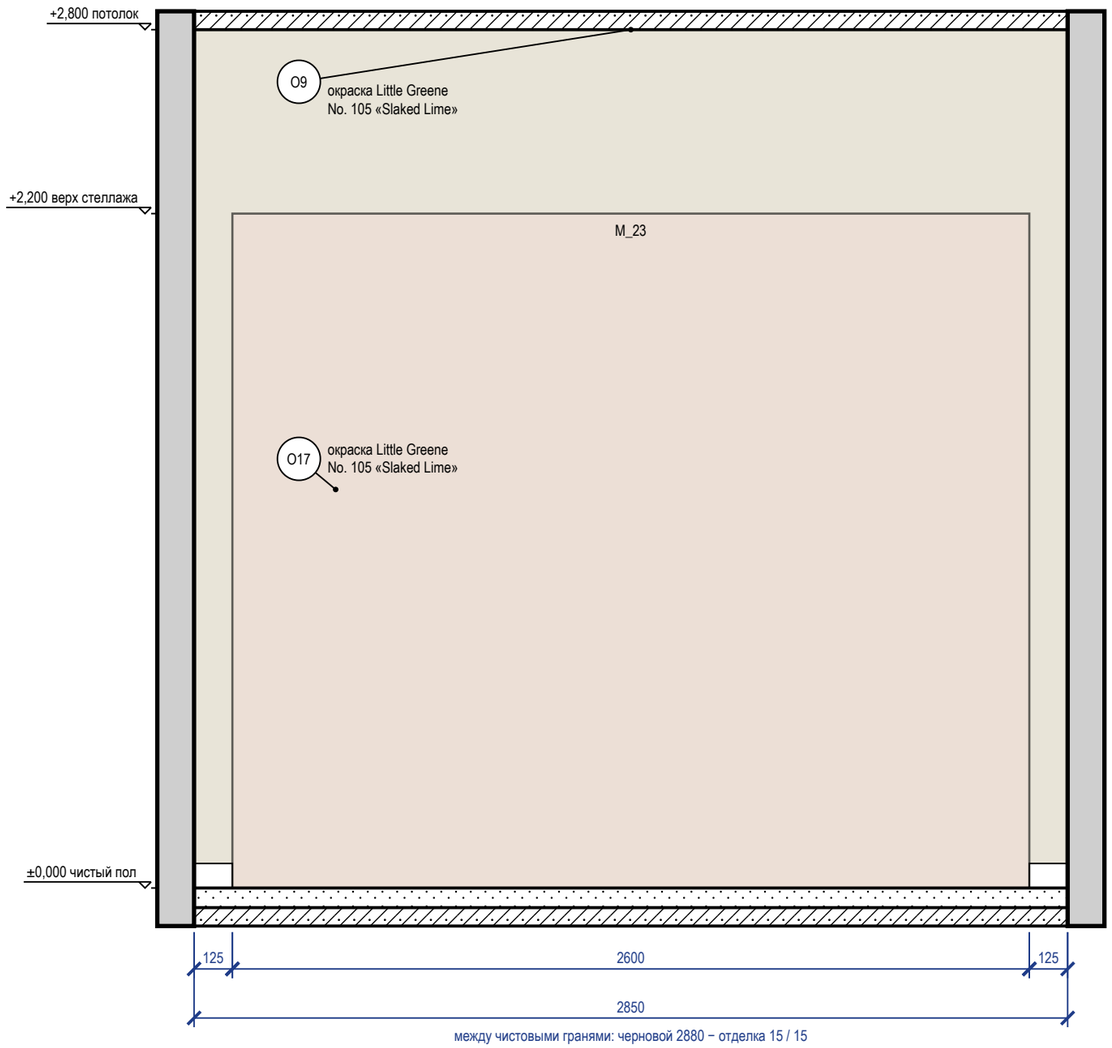


Схема развёрток (М 1:100)

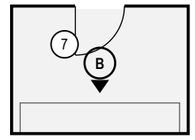

Ведомость отделки (на листе)

Марка	Поверхность	Материал, изделие	Цвет, код	Кол.
O9	потолок	окраска, Little Greene Absolute Matt, глубокоматовая, подготовка Q3	Little Greene No. 105 «Slaked Lime»	6 м²
O17	стены	окраска, Little Greene Intelligent Matt, матовая, подготовка Q3	Little Greene No. 105 «Slaked Lime»	8 м²
O18	плинтус	плинтус МДФ, h 80 мм, аналог: плинтус МДФ под покраску 80×16	Little Greene No. 105 «Slaked Lime»	0,3 м

Примечания

1. Размеры — в мм от чистовых поверхностей стен; условные обозначения и общие указания — лист 3.

					Проект: Дом 331 м²		М 1:20
	Лист	№ док.	Подпись	Дата	Развёртки стен. Кладовая (пом. 7)	Стадия	Лист	Листов
Дизайнер	Кырлан А.С.			04.11.26		П	99	168

Развёртка стены А


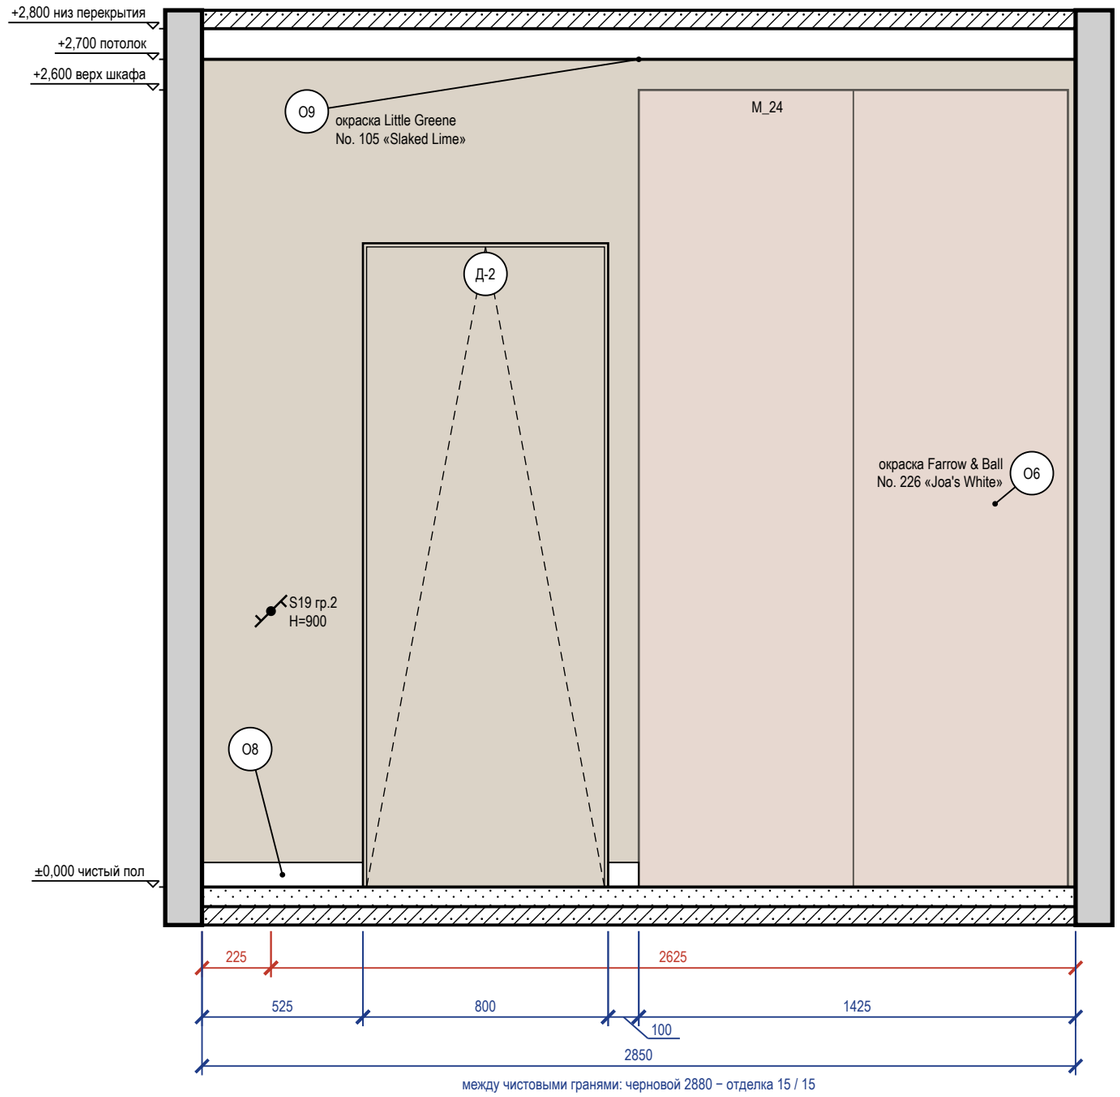


Схема развёрток (М 1:100)

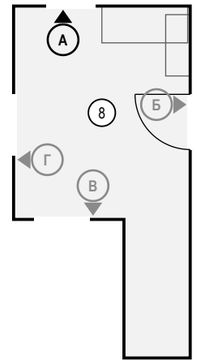

Ведомость отделки (на листе)

Марка	Поверхность	Материал, изделие	Цвет, код	Кол.
О6	стены	окраска, Farrow & Ball Modern Emulsion, матовая, подготовка Q3	Farrow & Ball No. 226 «Joa's White»	6 м²
О8	плинтус	плинтус МДФ, h 80 мм, аналог: плинтус МДФ под покраску 80×16	Farrow & Ball No. 226 «Joa's White»	0,6 м
О9	потолок	окраска, Little Greene Absolute Matt, глубокоматовая, подготовка Q3	Little Greene No. 105 «Slaked Lime»	12,5 м²

Примечания

1. Размеры — в мм от чистовых поверхностей стен; условные обозначения и общие указания — лист 3.
2. Двери скрытого монтажа — полотно в плоскости стены, отделка стены по полотну, плинтус прерывается у короба (узел — на листе узлов).

	Лист	№ док.	Подпись	Дата
Дизайнер	Кырлан А.С.			04.11.26

Проект: Дом 331 м² — **М 1:20**

Развёртка стены А. Прихожая (пом. 8)

Стадия	Лист	Листов
П	100	168

Развёртка стены Б


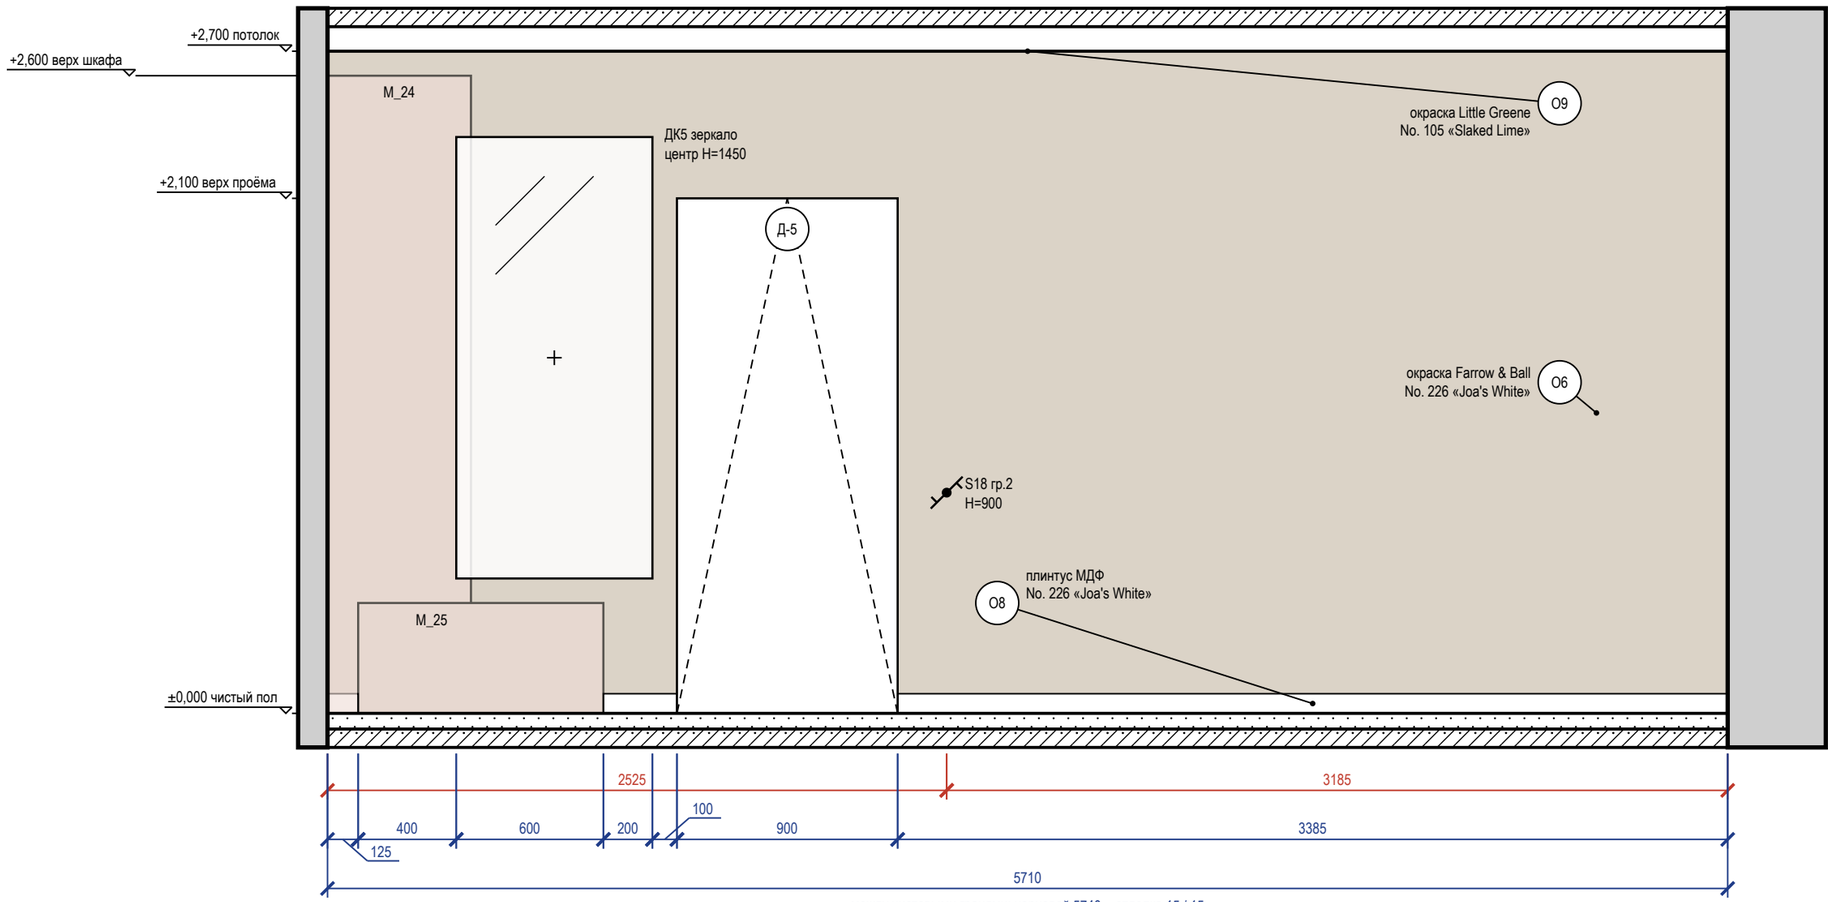


Схема развёрток (М 1:100)

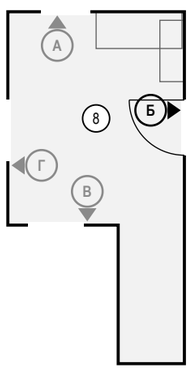

Ведомость отделки (на листе)

Марка	Поверхность	Материал, изделие	Цвет, код	Кол.
O6	стены	окраска, Farrow & Ball Modern Emulsion, матовая, подготовка Q3	Farrow & Ball No. 226 «Joa's White»	13,5 м²
O8	плинтус	плинтус МДФ, h 80 мм, аналог: плинтус МДФ под покраску 80×16	Farrow & Ball No. 226 «Joa's White»	3,8 м
O9	потолок	окраска, Little Greene Absolute Matt, глубокоматовая, подготовка Q3	Little Greene No. 105 «Slaked Lime»	12,5 м²

Примечания

1. Размеры — в мм от чистовых поверхностей стен; условные обозначения и общие указания — лист 3.
2. Картины и зеркала крепить к основанию по паспорту изделия (закладные и анкеры — в перечне скрытых работ); крест — ось центра предмета.

	Лист	№ док.	Подпись	Дата
Дизайнер	Кырлан А.С.			04.11.26

Проект: Дом 331 м² — М 1:25

Развёртка стены Б. Прихожая (пом. 8)

Стадия	Лист	Листов
П	101	168

выпуск 04.11.2026 № f163a372b2 · стр. 101 из 168

Развёртка стены В


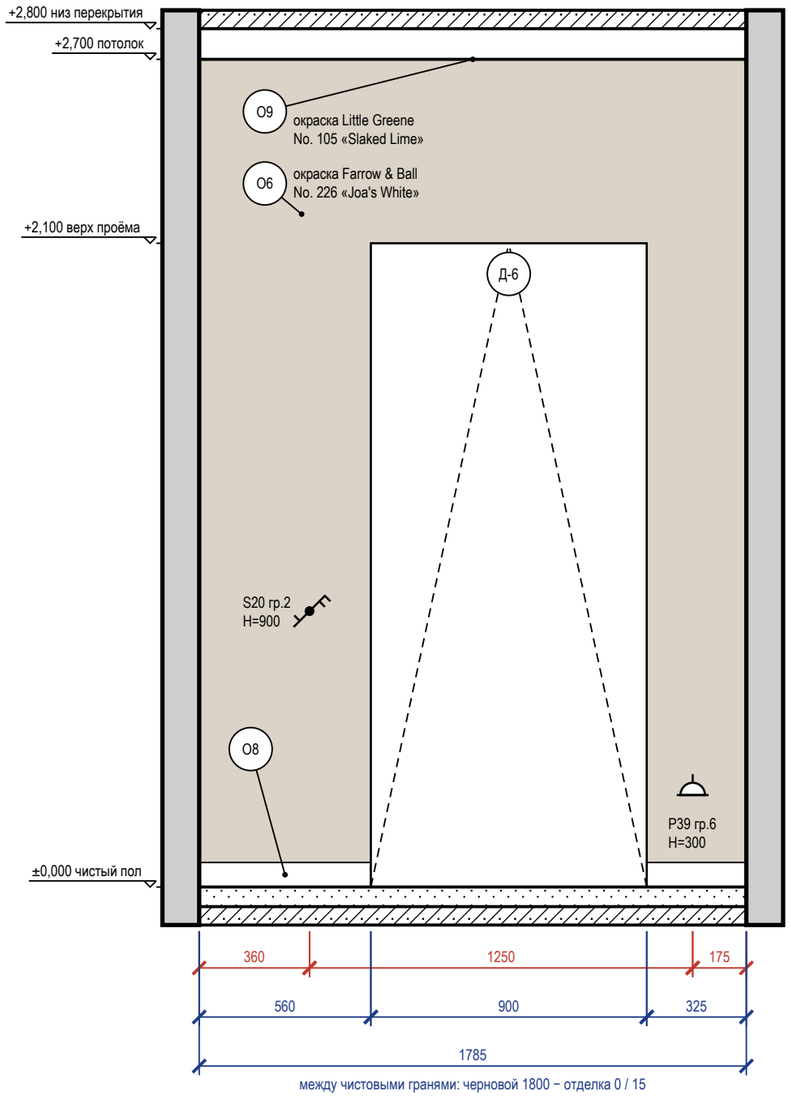


Схема развёрток (М 1:100)

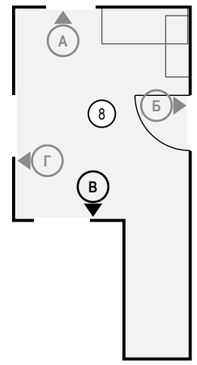

Ведомость отделки (на листе)

Марка	Поверхность	Материал, изделие	Цвет, код	Кол.
О6	стены	окраска, Farrow & Ball Modern Emulsion, матовая, подготовка Q3	Farrow & Ball No. 226 «Joa's White»	2,9 м²
О8	плинтус	плинтус МДФ, h 80 мм, аналог: плинтус МДФ под покраску 80×16	Farrow & Ball No. 226 «Joa's White»	0,9 м
О9	потолок	окраска, Little Greene Absolute Matt, глубокоматовая, подготовка Q3	Little Greene No. 105 «Slaked Lime»	12,5 м²

Примечания

1. Размеры — в мм от чистовых поверхностей стен; условные обозначения и общие указания — лист 3.

					Проект: Дом 331 м²	М 1:20
	Лист	№ док.	Подпись	Дата		
Дизайнер	Кырлан А.С.			04.11.26	Развёртка стены В. Прихожая (пом. 8)	
					Стадия: П	Лист: 102 / Листов: 168

Развёртка стены Г


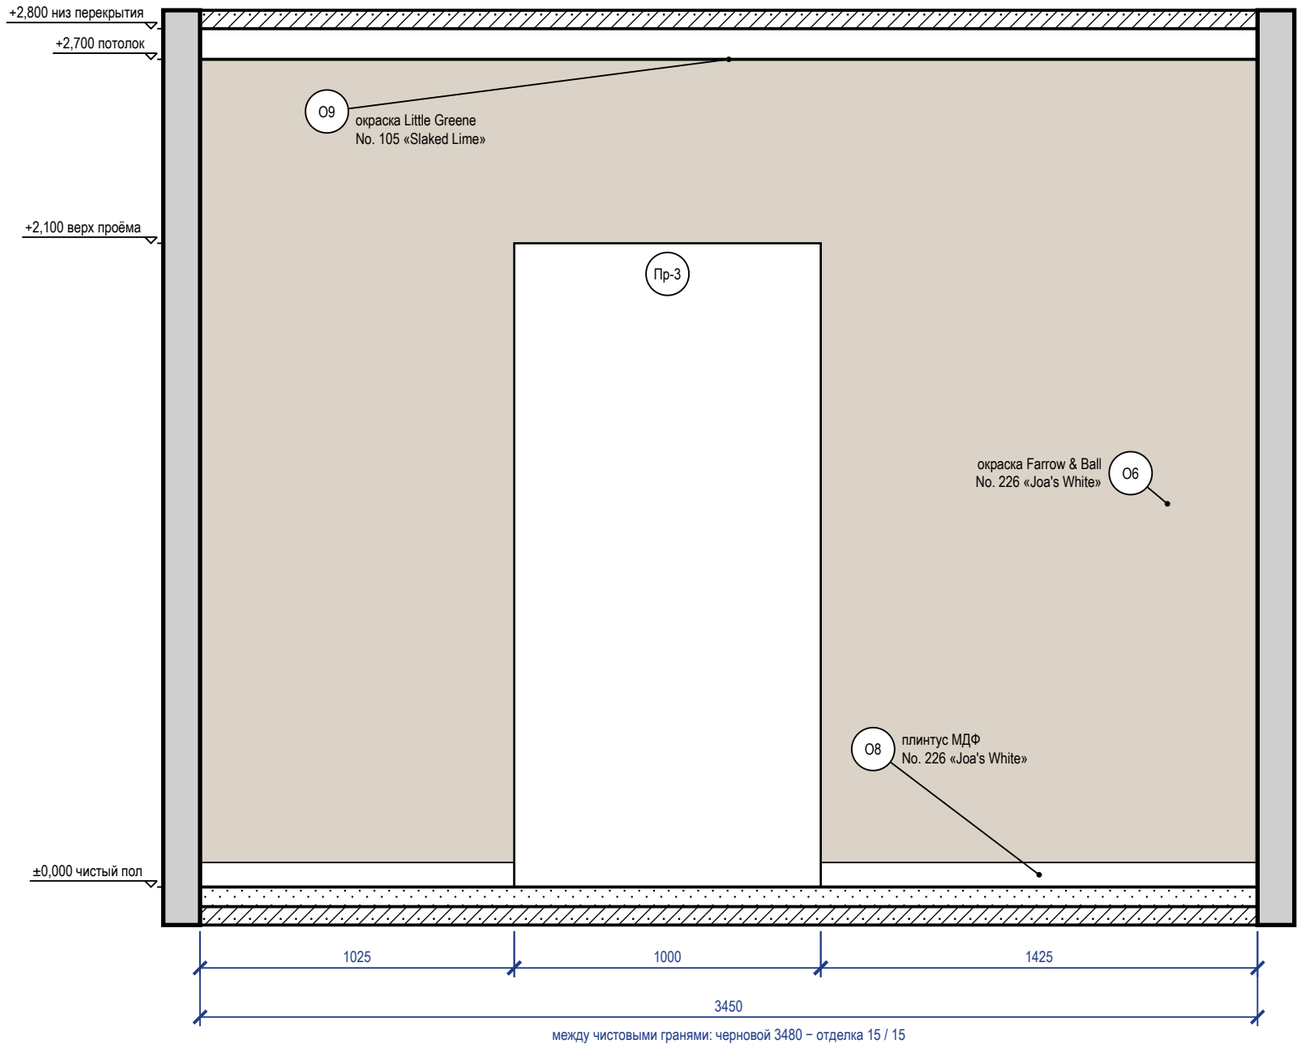


Схема развёрток (М 1:100)

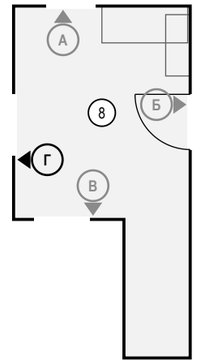

Ведомость отделки (на листе)

Марка	Поверхность	Материал, изделие	Цвет, код	Кол.
О6	стены	окраска, Farrow & Ball Modern Emulsion, матовая, подготовка Q3	Farrow & Ball No. 226 «Joa's White»	7,2 м²
О8	плинтус	плинтус МДФ, h 80 мм, аналог: плинтус МДФ под покраску 80×16	Farrow & Ball No. 226 «Joa's White»	2,5 м
О9	потолок	окраска, Little Greene Absolute Matt, глубокоматовая, подготовка Q3	Little Greene No. 105 «Slaked Lime»	12,5 м²

Примечания

1. Размеры — в мм от чистовых поверхностей стен; условные обозначения и общие указания — лист 3.
2. Стена Г показана двумя видами: здесь — архитектурная развёртка (мебель, отделка, проёмы, высоты), электроточки и выводы ВК с привязками и таблицей — на листе 104 («Привязки»).

					Проект: Дом 331 м²	М 1:20
	Лист	№ док.	Подпись	Дата	Развёртка стены Г. Прихожая (пом. 8)	Стадия / Лист / Листов
Дизайнер	Кырлан А.С.			04.11.26		П / 103 / 168

Развёртка стены Г: электроточки и выводы

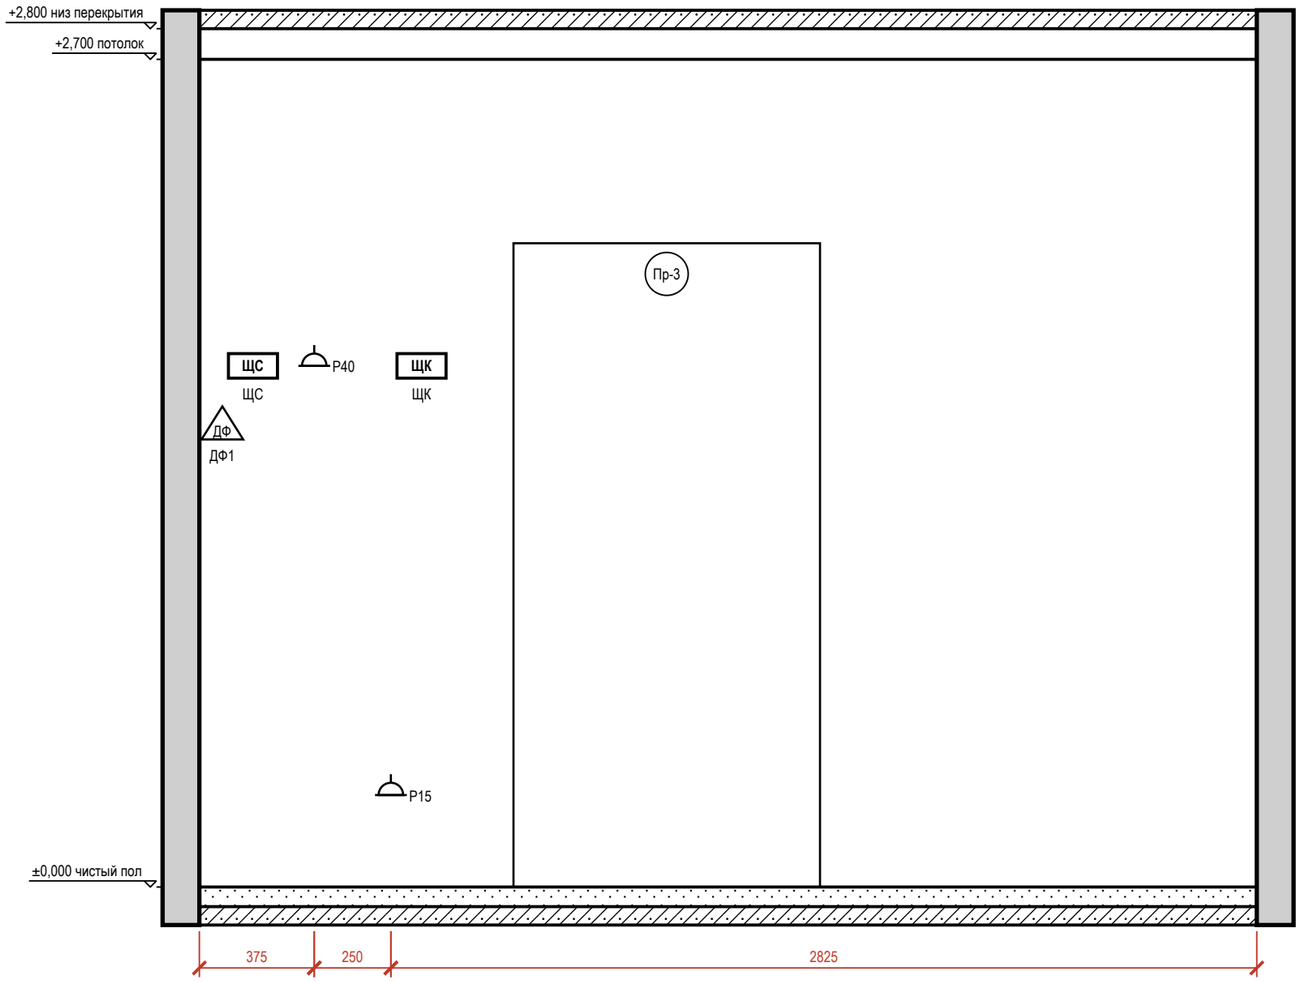



Таблица привязок электроточек и выводов

Марка	Назначение	От угла, мм	Н от пола, мм	Примечание
ДФ1	домофон: трубка домофона	75	1500	
ЩС	щит: щит слаботочный: ввод оптики, ONT, роутер, патч-панель	175	1700	
Р40	розетка: питание слаботочного щита (рядом с ЩС)	375	1700	гр. 14
Р15	розетка: пылесос, сушилка обуви	625	300	гр. 6
ЩК	щит: щит квартирный ЩРВ-П-48	725	1700	

Условные обозначения

- розетка с заземляющим контактом; у знака — марка, ×N постов в рамке, гр. — группа щита, Н — высота оси, мм
- ДФ — трубка или монитор домофона
- ЩК — щит квартирный
- привязки точек и выводов от угла и от пола, мм
- А — марка развёртки: буква стены, стрелка — взгляд

Схема развёрток (М 1:50)

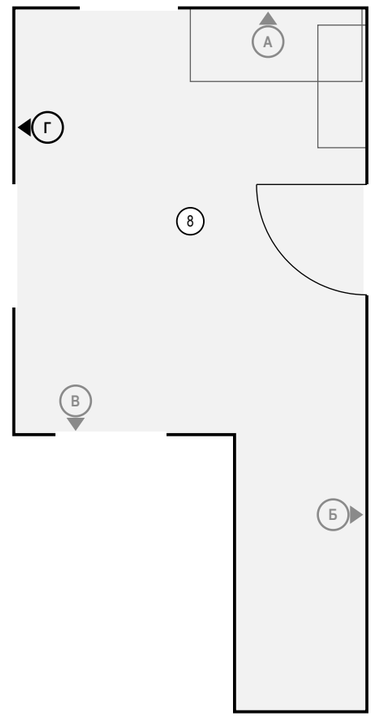

Примечания

1. Вид «Привязки» стены Г — электроточки и выводы ВК; архитектурная развёртка (мебель, отделка, проёмы, высоты) — на листе 103. Мебель и приборы — подложкой для ориентира; их марки и обозначения мебели, проёмов и стен — там же.
2. Привязки — в мм: по горизонтали от левого чистового угла стены до оси изделия, Н — от чистого пола до оси; все точки — в таблице привязок. Красная цепочка — привязки по осям; точки ближе 120 мм одна к другой в цепочку не дробятся — их привязки только в таблице.
3. У знака — марка электроточки (Р — розетка, S — выключатель, Св — светильник, ЭВ — вывод кабеля); условные обозначения и общие указания — лист 3.

	Лист	№ док.	Подпись	Дата
Дизайнер	Кырлан А.С.			04.11.26

Проект: Дом 331 м² — **М 1:20**

Привязки электроточек, стена Г. Прихожая (пом. 8)

Стадия	Лист	Листов
П	104	168

Развёртка стены Г


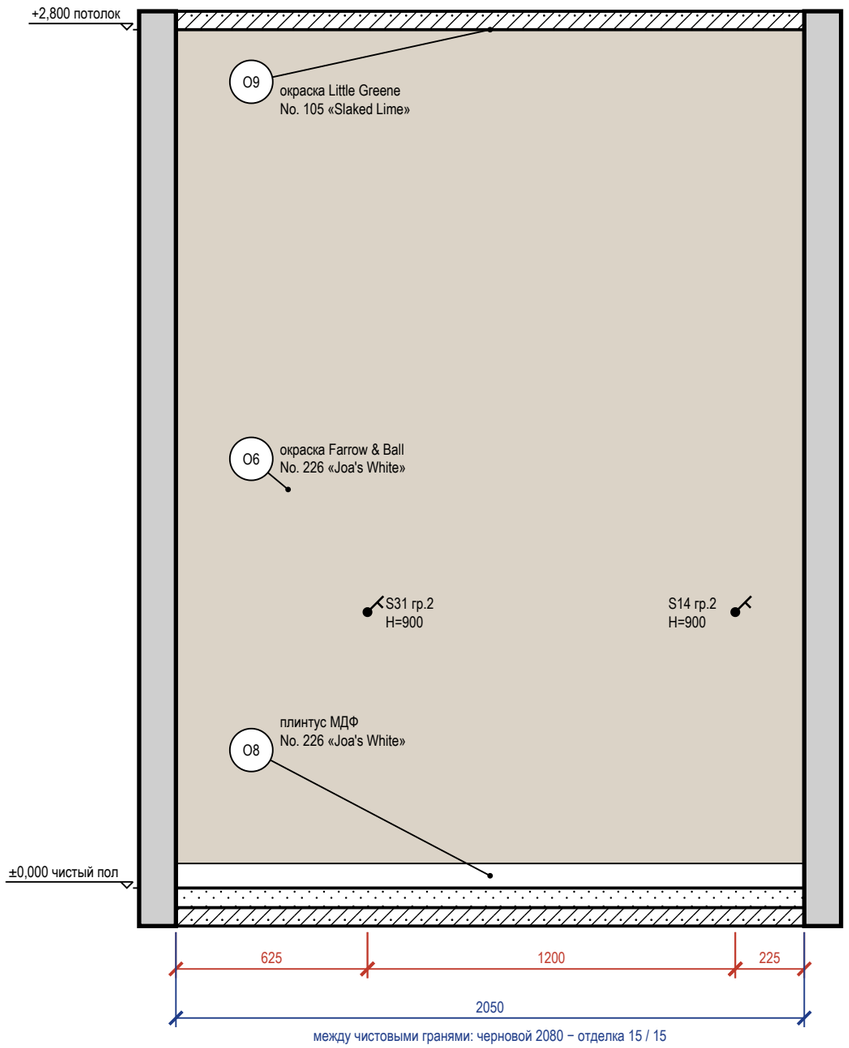


Схема развёрток (М 1:100)

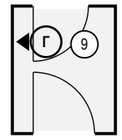

Ведомость отделки (на листе)

Марка	Поверхность	Материал, изделие	Цвет, код	Кол.
О6	стены	окраска, Farrow & Ball Modern Emulsion, матовая, подготовка Q3	Farrow & Ball No. 226 «Joa's White»	5,7 м²
О8	плинтус	плинтус МДФ, h 80 мм, аналог: плинтус МДФ под покраску 80×16	Farrow & Ball No. 226 «Joa's White»	2 м
О9	потолок	окраска, Little Greene Absolute Matt, глубокоматовая, подготовка Q3	Little Greene No. 105 «Slaked Lime»	3,5 м²

Примечания

1. Размеры — в мм от чистовых поверхностей стен; условные обозначения и общие указания — лист 3.

					Проект: Дом 331 м²	М 1:20
	Лист	№ док.	Подпись	Дата		
Дизайнер	Кырлан А.С.			04.11.26	Развёртки стен. Тамбур (пом. 9)	Стадия: П; Лист: 105; Листов: 168

Развёртка стены А


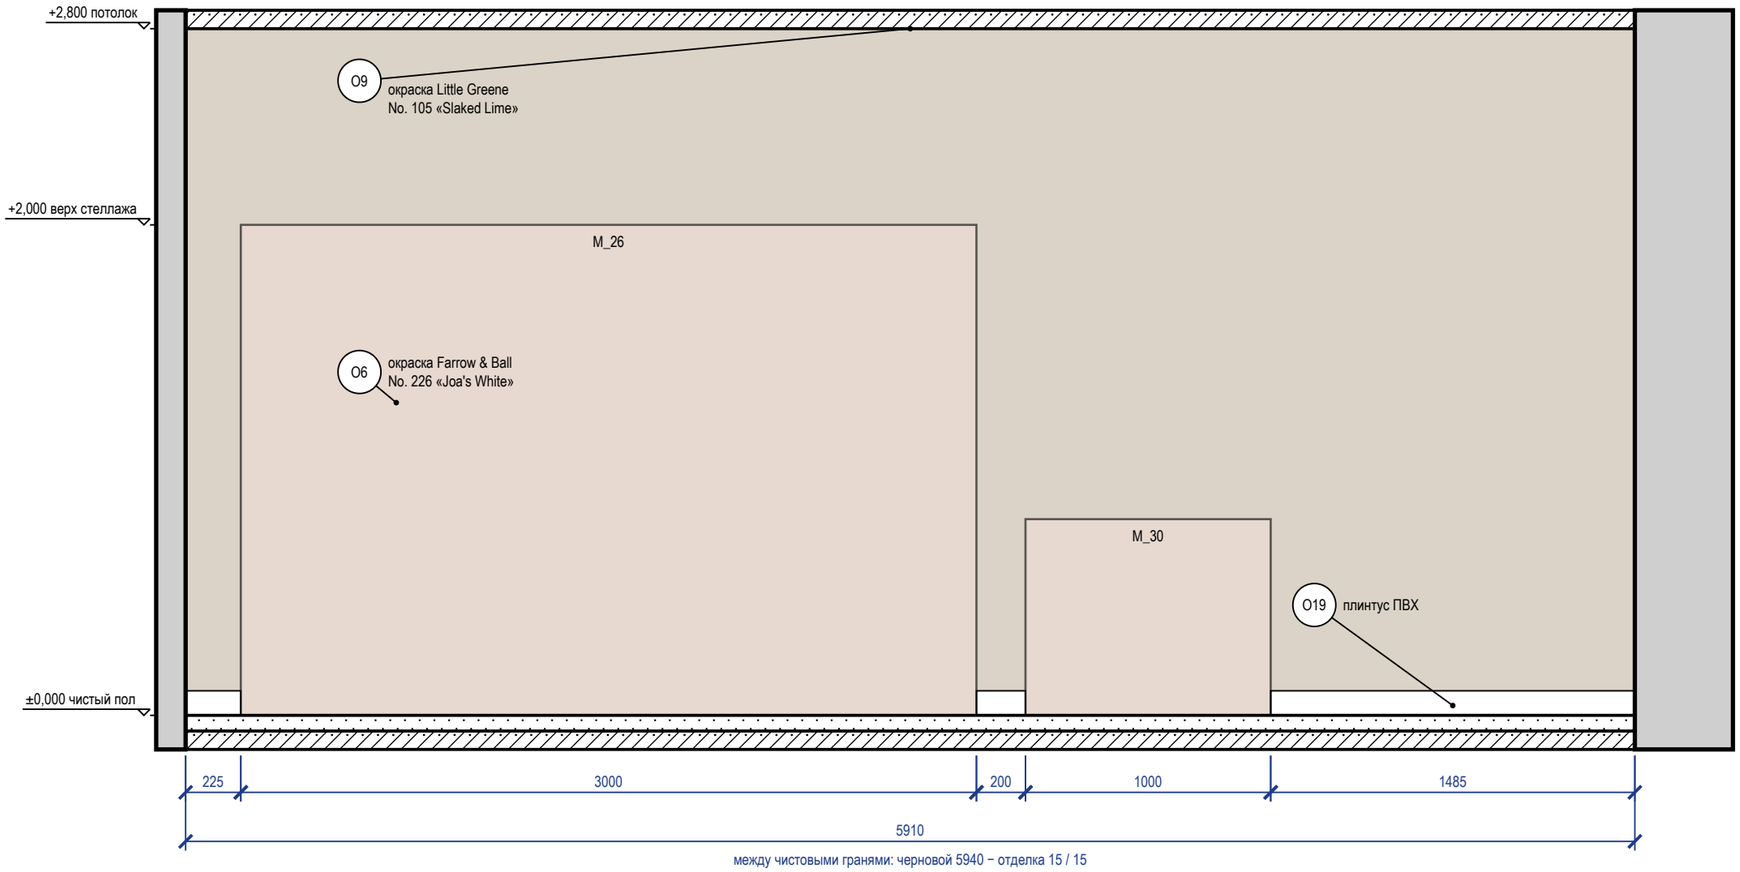


Схема развёрток (М 1:100)

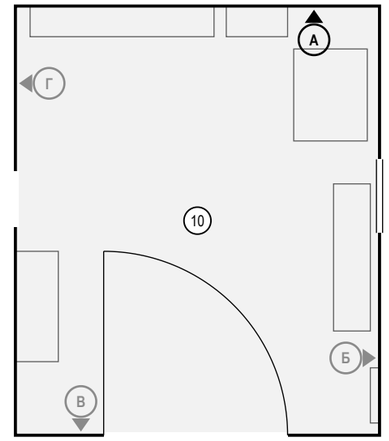

Ведомость отделки (на листе)

Марка	Поверхность	Материал, изделие	Цвет, код	Кол.
О6	стены	окраска, Farrow & Ball Modern Emulsion, матовая, подготовка Q3	Farrow & Ball No. 226 «Joa's White»	16,5 м²
О9	потолок	окраска, Little Greene Absolute Matt, глубокоматовая, подготовка Q3	Little Greene No. 105 «Slaked Lime»	41,6 м²
О19	плинтус	плинтус ПВХ, h 100 мм, аналог: плинтус ПВХ влагостойкий 100 мм, серый		1,9 м

Примечания

1. Размеры — в мм от чистовых поверхностей стен; условные обозначения и общие указания — лист 3.

					Проект: Дом 331 м² — М 1:25
	Лист	№ док.	Подпись	Дата	Развёртка стены А. Гараж (пом. 10)
Дизайнер	Кырлан А.С.			04.11.26	Стадия: П; Лист: 106; Листов: 168

Развёртка стены Б


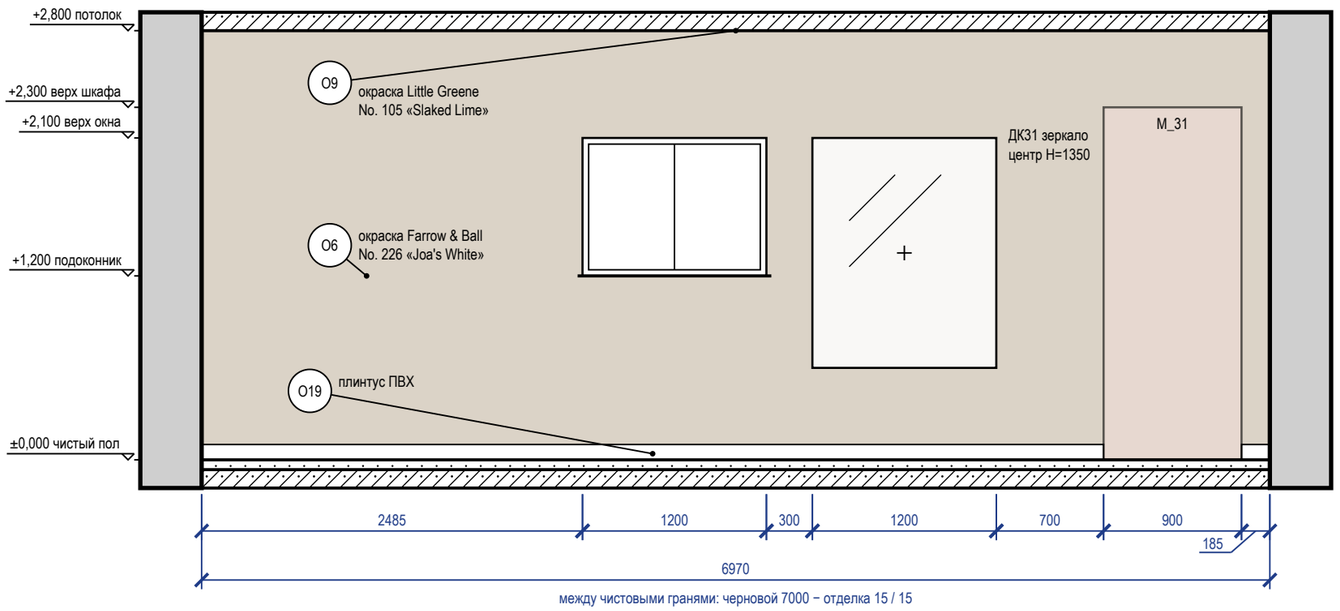


Схема развёрток (М 1:100)

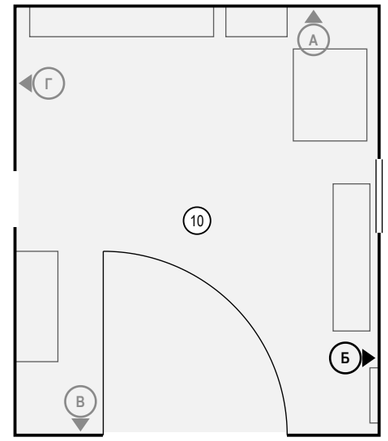

Ведомость отделки (на листе)

Марка	Поверхность	Материал, изделие	Цвет, код	Кол.
О6	стены	окраска, Farrow & Ball Modern Emulsion, матовая, подготовка Q3	Farrow & Ball No. 226 «Joa's White»	18,4 м²
О9	потолок	окраска, Little Greene Absolute Matt, глубокоматовая, подготовка Q3	Little Greene No. 105 «Slaked Lime»	41,6 м²
О19	плинтус	плинтус ПВХ, h 100 мм, аналог: плинтус ПВХ влагостойкий 100 мм, серый		6,1 м

Примечания

1. Размеры — в мм от чистовых поверхностей стен; условные обозначения и общие указания — лист 3.
2. Картины и зеркала крепить к основанию по паспорту изделия (закладные и анкеры — в перечне скрытых работ); крест — ось центра предмета.

	Лист	№ док.	Подпись	Дата
Дизайнер	Кырлан А.С.			04.11.26

Проект: Дом 331 м² — **М 1:40**

Развёртка стены Б. Гараж (пом. 10)

Стадия	Лист	Листов
П	107	168

Развёртка стены В


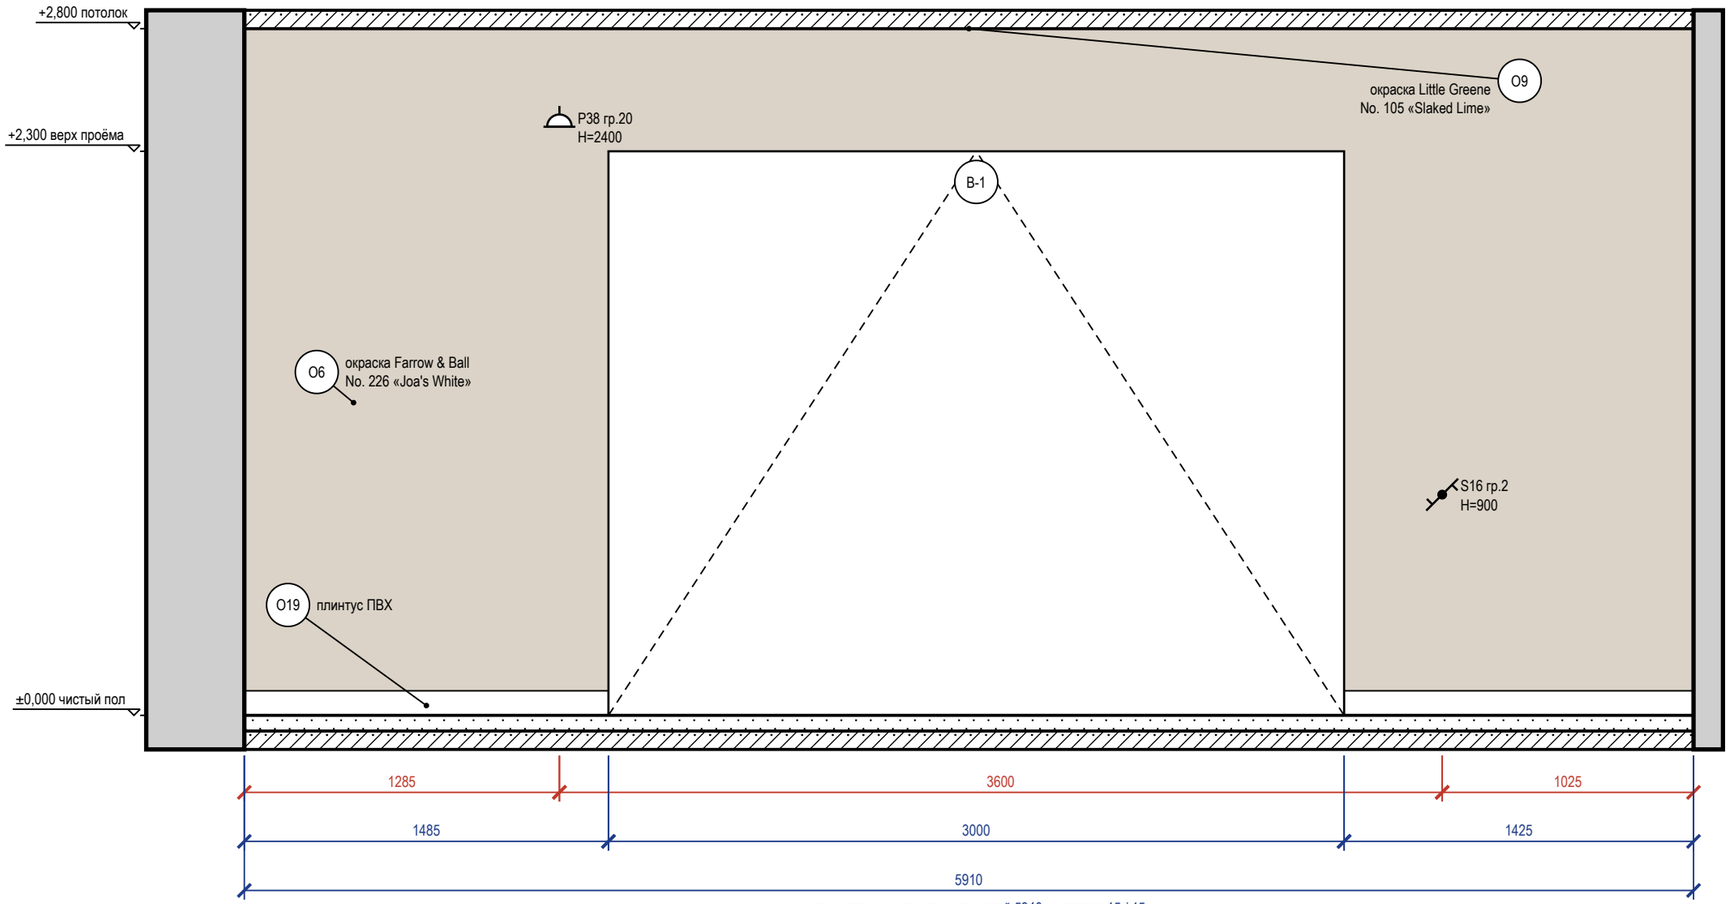


Схема развёрток (М 1:100)

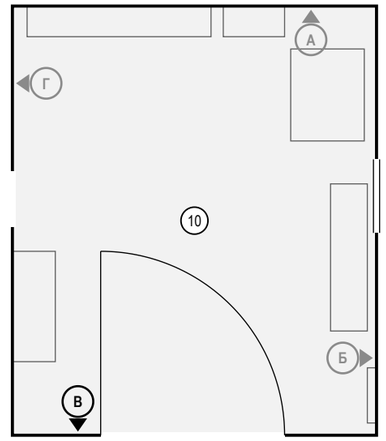

Ведомость отделки (на листе)


Марка	Поверхность	Материал, изделие	Цвет, код	Кол.
O6	стены	окраска, Farrow & Ball Modern Emulsion, матовая, подготовка Q3	Farrow & Ball No. 226 «Joa's White»	9,6 м²
O9	потолок	окраска, Little Greene Absolute Matt, глубокоматовая, подготовка Q3	Little Greene No. 105 «Slaked Lime»	41,6 м²
O19	плинтус	плинтус ПВХ, h 100 мм, аналог: плинтус ПВХ влагостойкий 100 мм, серый		2,9 м

Примечания

1. Размеры — в мм от чистовых поверхностей стен; условные обозначения и общие указания — лист 3.


					Проект: Дом 331 м² — М 1:25
	Лист	№ док.	Подпись	Дата	
Дизайнер	Кырлан А.С.			04.11.26	Развёртка стены В. Гараж (пом. 10)
					Стадия: П; Лист: 108; Листов: 168

Развёртка стены Г

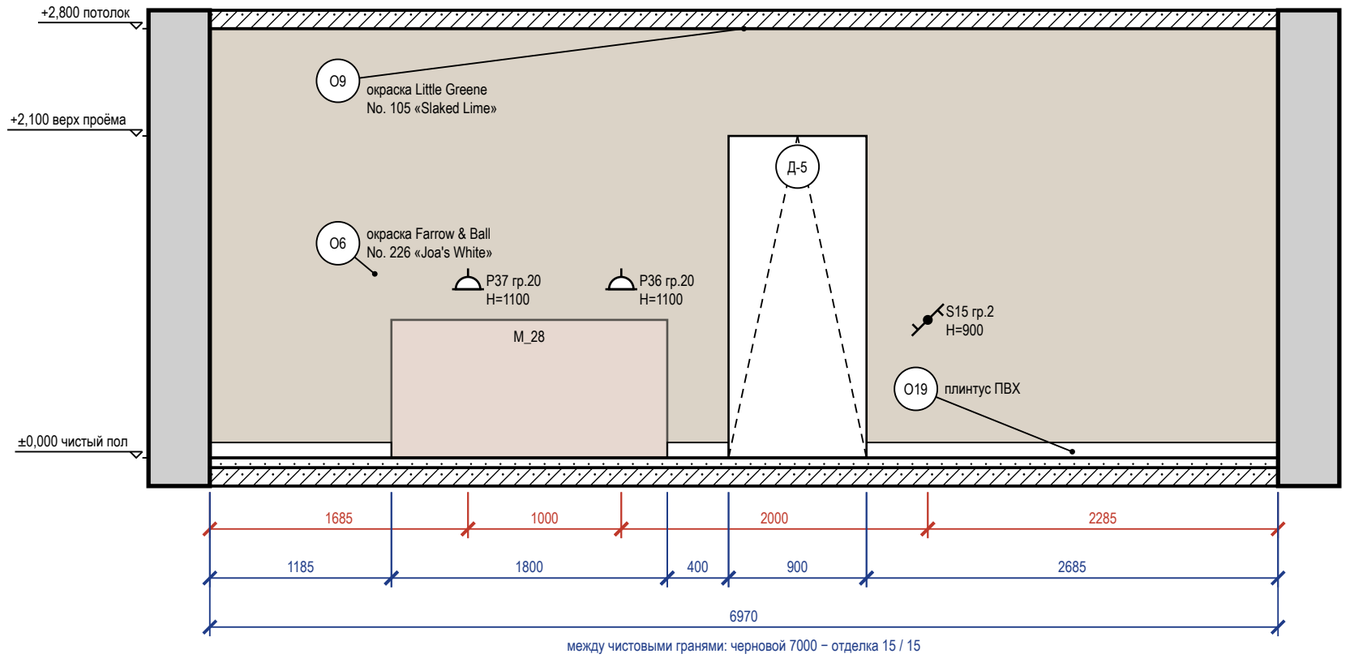

между чистовыми гранями: черновой 7000 − отделка 15 / 15

Схема развёрток (М 1:100)

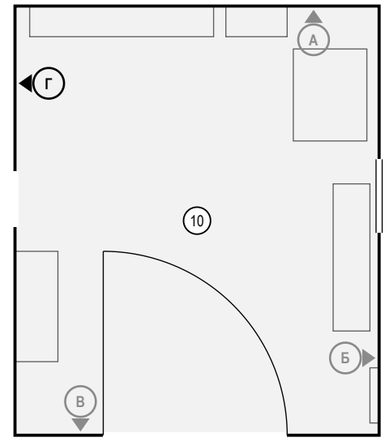

Ведомость отделки (на листе)

Марка	Поверхность	Материал, изделие	Цвет, код	Кол.
О6	стены	окраска, Farrow & Ball Modern Emulsion, матовая, подготовка Q3	Farrow & Ball No. 226 «Joa's White»	17,6 м²
О9	потолок	окраска, Little Greene Absolute Matt, глубокоматовая, подготовка Q3	Little Greene No. 105 «Slaked Lime»	41,6 м²
О19	плинтус	плинтус ПВХ, h 100 мм, аналог: плинтус ПВХ влагостойкий 100 мм, серый		4,3 м

Примечания

1. Размеры — в мм от чистовых поверхностей стен; условные обозначения и общие указания — лист 3.

	Лист	№ док.	Подпись	Дата
Дизайнер	Кырлан А.С.			04.11.26

Проект: Дом 331 м² — **М 1:40**

Развёртка стены Г. Гараж (пом. 10)

Стадия	Лист	Листов
П	109	168

Развёртка стены А


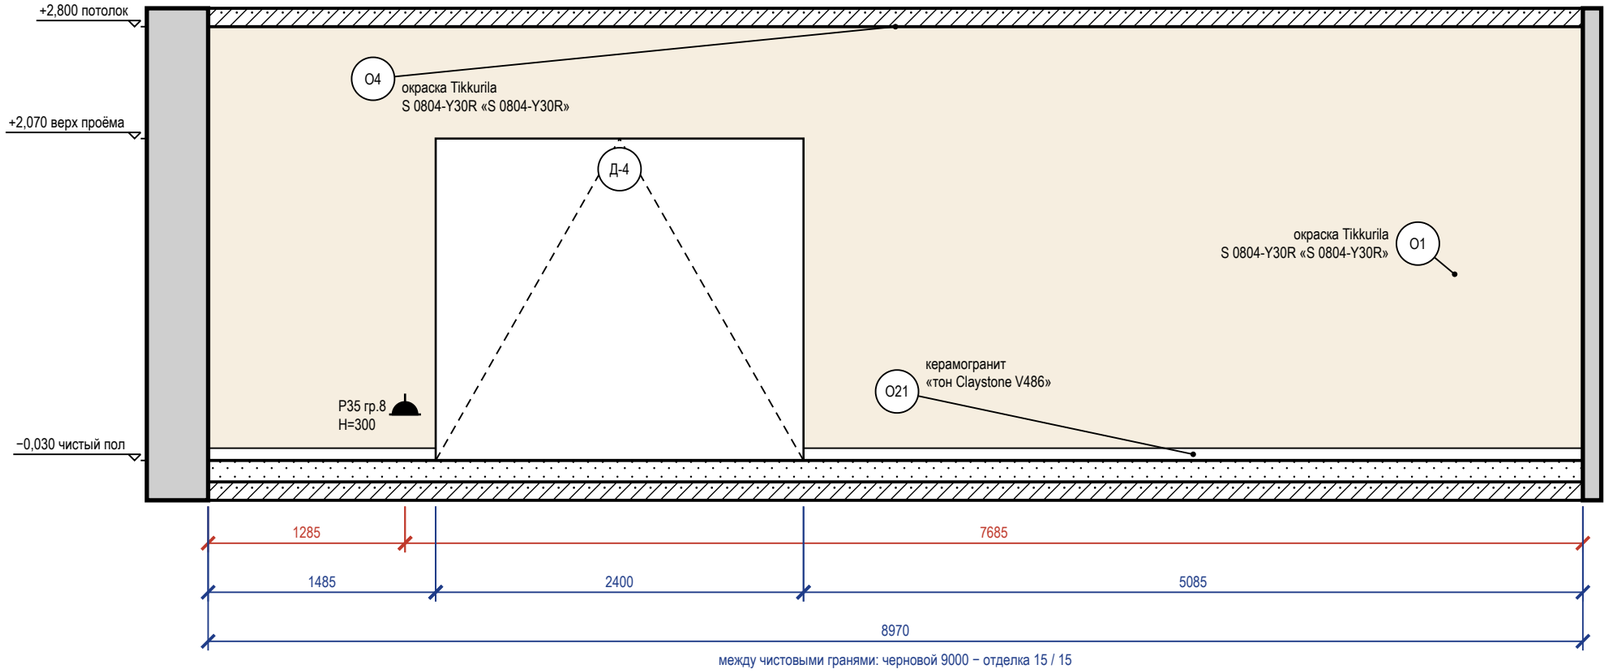


Схема развёрток (М 1:100)

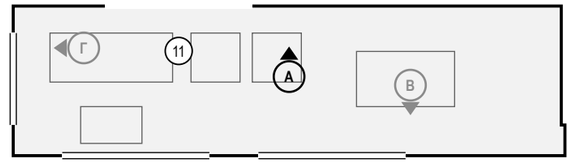

Ведомость отделки (на листе)

Марка	Поверхность	Материал, изделие	Цвет, код	Кол.
О1	стены	окраска, Tikkurila Luja 7, шелковисто-матовая, подготовка К3	NCS S 0804-Y30R «S 0804-Y30R»	20,3 м²
О4	потолок	окраска, Tikkurila Luja 7, матовая, подготовка Q3	NCS S 0804-Y30R «S 0804-Y30R»	21,8 м²
О21	плинтус	керамогранит, аналог: плинтус из керамогранита пола, подрезка 80 мм, верхняя кромка с запилом 45°	#B8AFA5 «тон Claystone V486»	6,6 м

Примечания

1. Размеры — в мм от чистовых поверхностей стен; условные обозначения и общие указания — лист 3.

					Проект: Дом 331 м²	М 1:40
	Лист	№ док.	Подпись	Дата		
Дизайнер	Кырлан А.С.			04.11.26	Развёртка стены А. Веранда (пом. 11)	
					Стадия: П	Лист: 110
						Листов: 168

Развёртка стены В


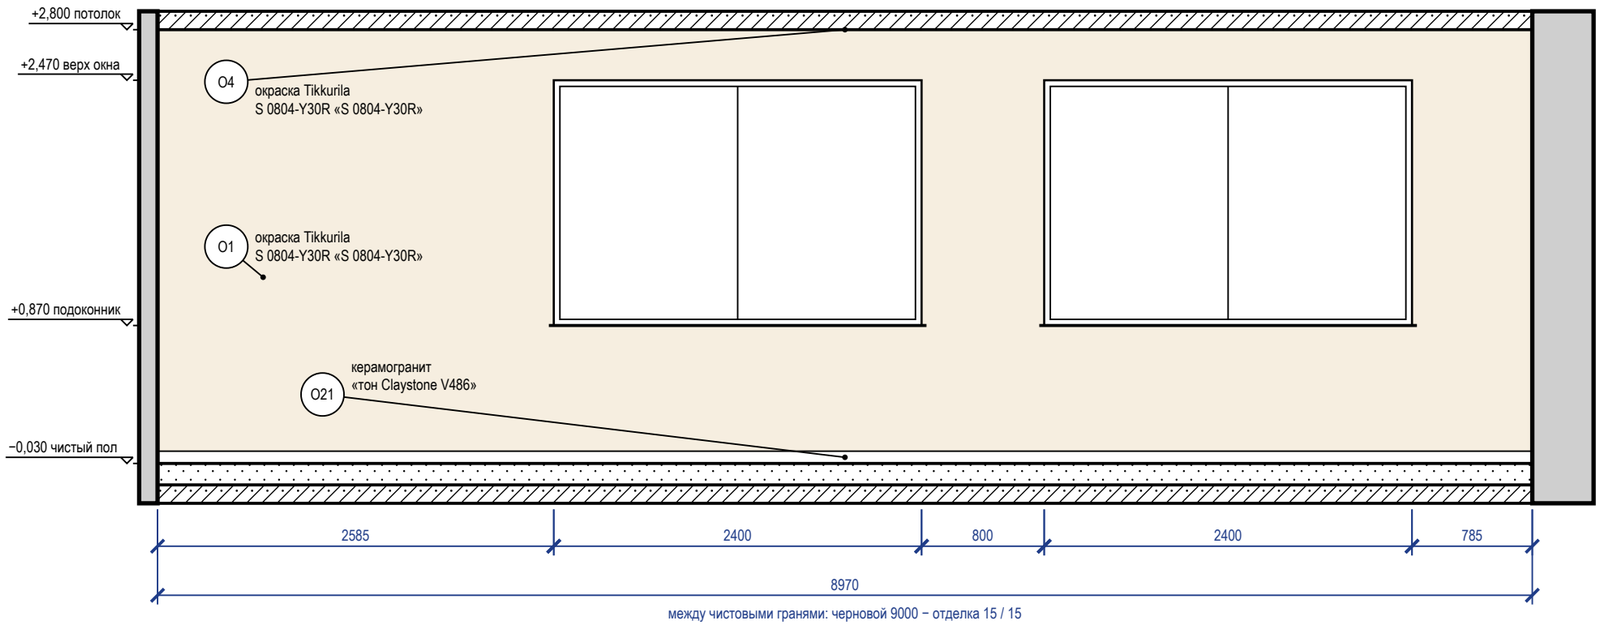


Схема развёрток (М 1:100)

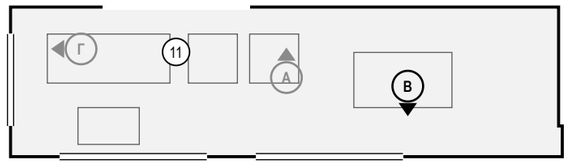

Ведомость отделки (на листе)

Марка	Поверхность	Материал, изделие	Цвет, код	Кол.
О1	стены	окраска, Tikkurila Luja 7, шелковисто-матовая, подготовка К3	NCS S 0804-Y30R «S 0804-Y30R»	17,7 м²
О4	потолок	окраска, Tikkurila Luja 7, матовая, подготовка Q3	NCS S 0804-Y30R «S 0804-Y30R»	21,8 м²
О21	плинтус	керамогранит, аналог: плинтус из керамогранита пола, подрезка 80 мм, верхняя кромка с запилом 45°	#B8AFA5 «тон Claystone V486»	9 м

Примечания

1. Размеры — в мм от чистовых поверхностей стен; условные обозначения и общие указания — лист 3.

					Проект: Дом 331 м²	М 1:40
	Лист	№ док.	Подпись	Дата		
Дизайнер	Кырлан А.С.			04.11.26	Развёртка стены В. Веранда (пом. 11)	

Стадия	Лист	Листов
П	111	168

Развёртка стены Г


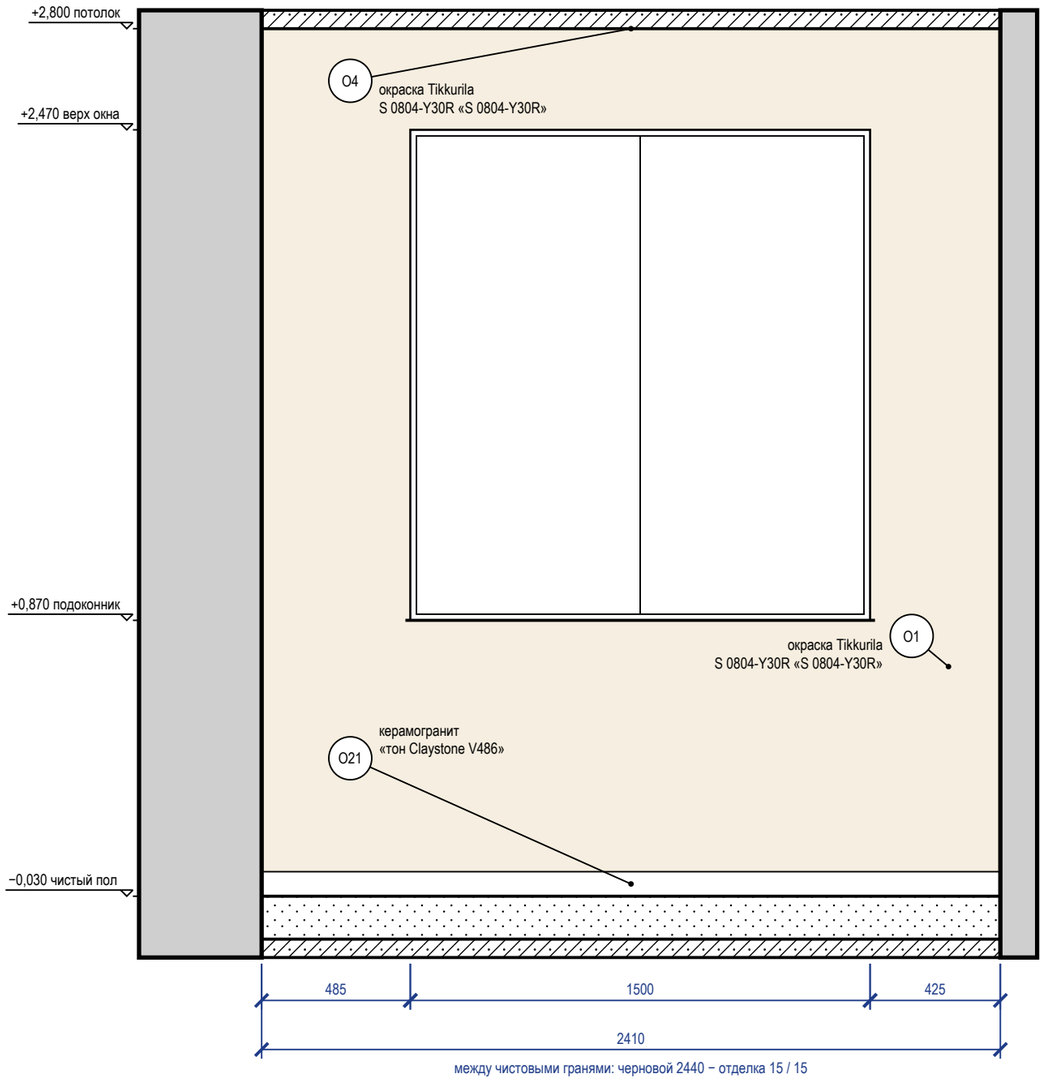


Схема развёрток (М 1:100)

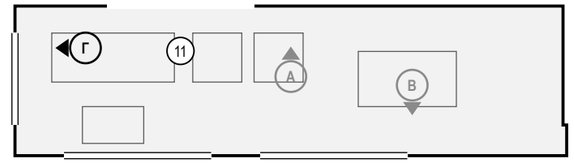

Ведомость отделки (на листе)

Марка	Поверхность	Материал, изделие	Цвет, код	Кол.
О1	стены	окраска, Tikkurila Luja 7, шелковисто-матовая, подготовка К3	NCS S 0804-Y30R «S 0804-Y30R»	4,4 м²
О4	потолок	окраска, Tikkurila Luja 7, матовая, подготовка Q3	NCS S 0804-Y30R «S 0804-Y30R»	21,8 м²
О21	плинтус	керамогранит, аналог: плинтус из керамогранита пола, подрезка 80 мм, верхняя кромка с запилом 45°	#B8AFA5 «тон Claystone V486»	2,4 м

Примечания

1. Размеры — в мм от чистовых поверхностей стен; условные обозначения и общие указания — лист 3.

					Проект: Дом 331 м²	М 1:20
	Лист	№ док.	Подпись	Дата		
Дизайнер	Кырлан А.С.			04.11.26	Развёртка стены Г. Веранда (пом. 11)	Стадия: П; Лист: 112; Листов: 168

Развёртка стены А


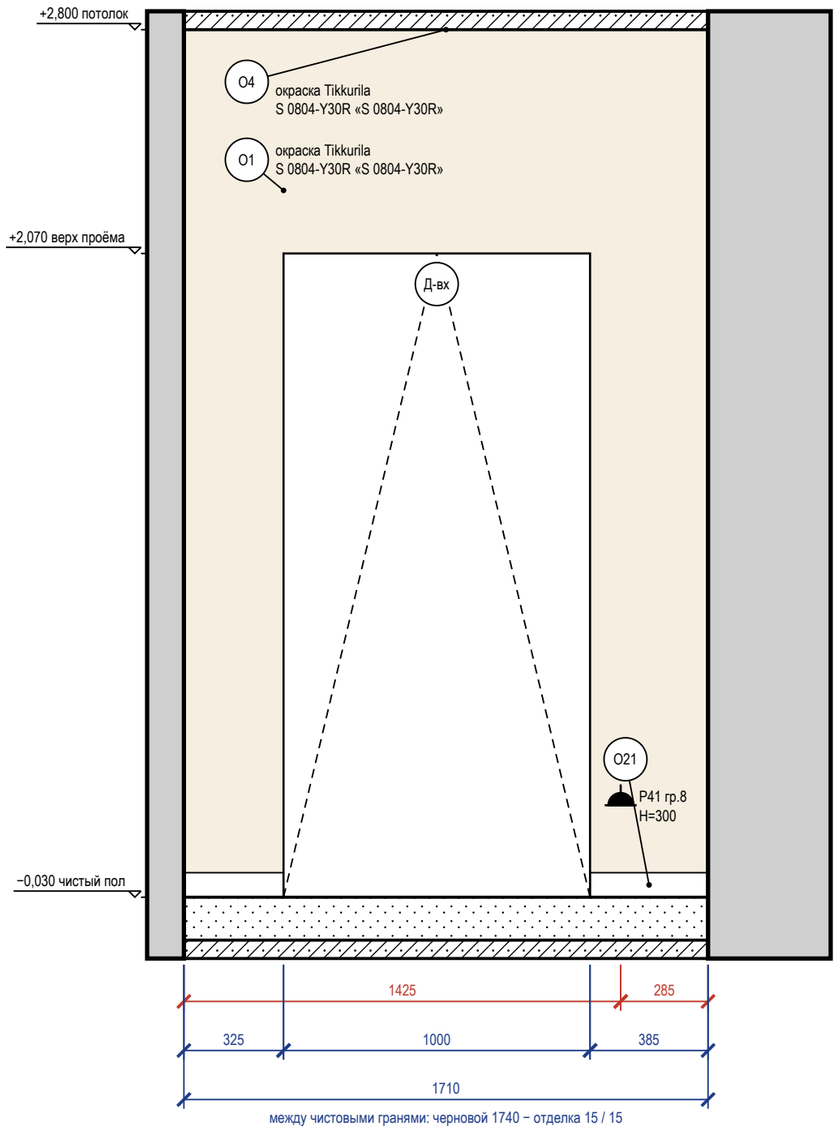


Схема развёрток (М 1:100)

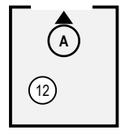

Ведомость отделки (на листе)

Марка	Поверхность	Материал, изделие	Цвет, код	Кол.
O1	стены	окраска, Tikkurila Luja 7, шелковисто-матовая, подготовка К3	NCS S 0804-Y30R «S 0804-Y30R»	2,7 м²
O4	потолок	окраска, Tikkurila Luja 7, матовая, подготовка Q3	NCS S 0804-Y30R «S 0804-Y30R»	3,4 м²
O21	плинтус	керамогранит, аналог: плинтус из керамогранита пола, подрезка 80 мм, верхняя кромка с запилом 45°	#B8AFA5 «тон Claystone V486»	0,7 м

Примечания

1. Размеры — в мм от чистовых поверхностей стен; условные обозначения и общие указания — лист 3.

					Проект: Дом 331 м²	М 1:20
	Лист	№ док.	Подпись	Дата		
Дизайнер	Кырлан А.С.			04.11.26	Развёртки стен. Крыльцо (пом. 12)	Стадия: П; Лист: 113; Листов: 168

Развёртка стены А


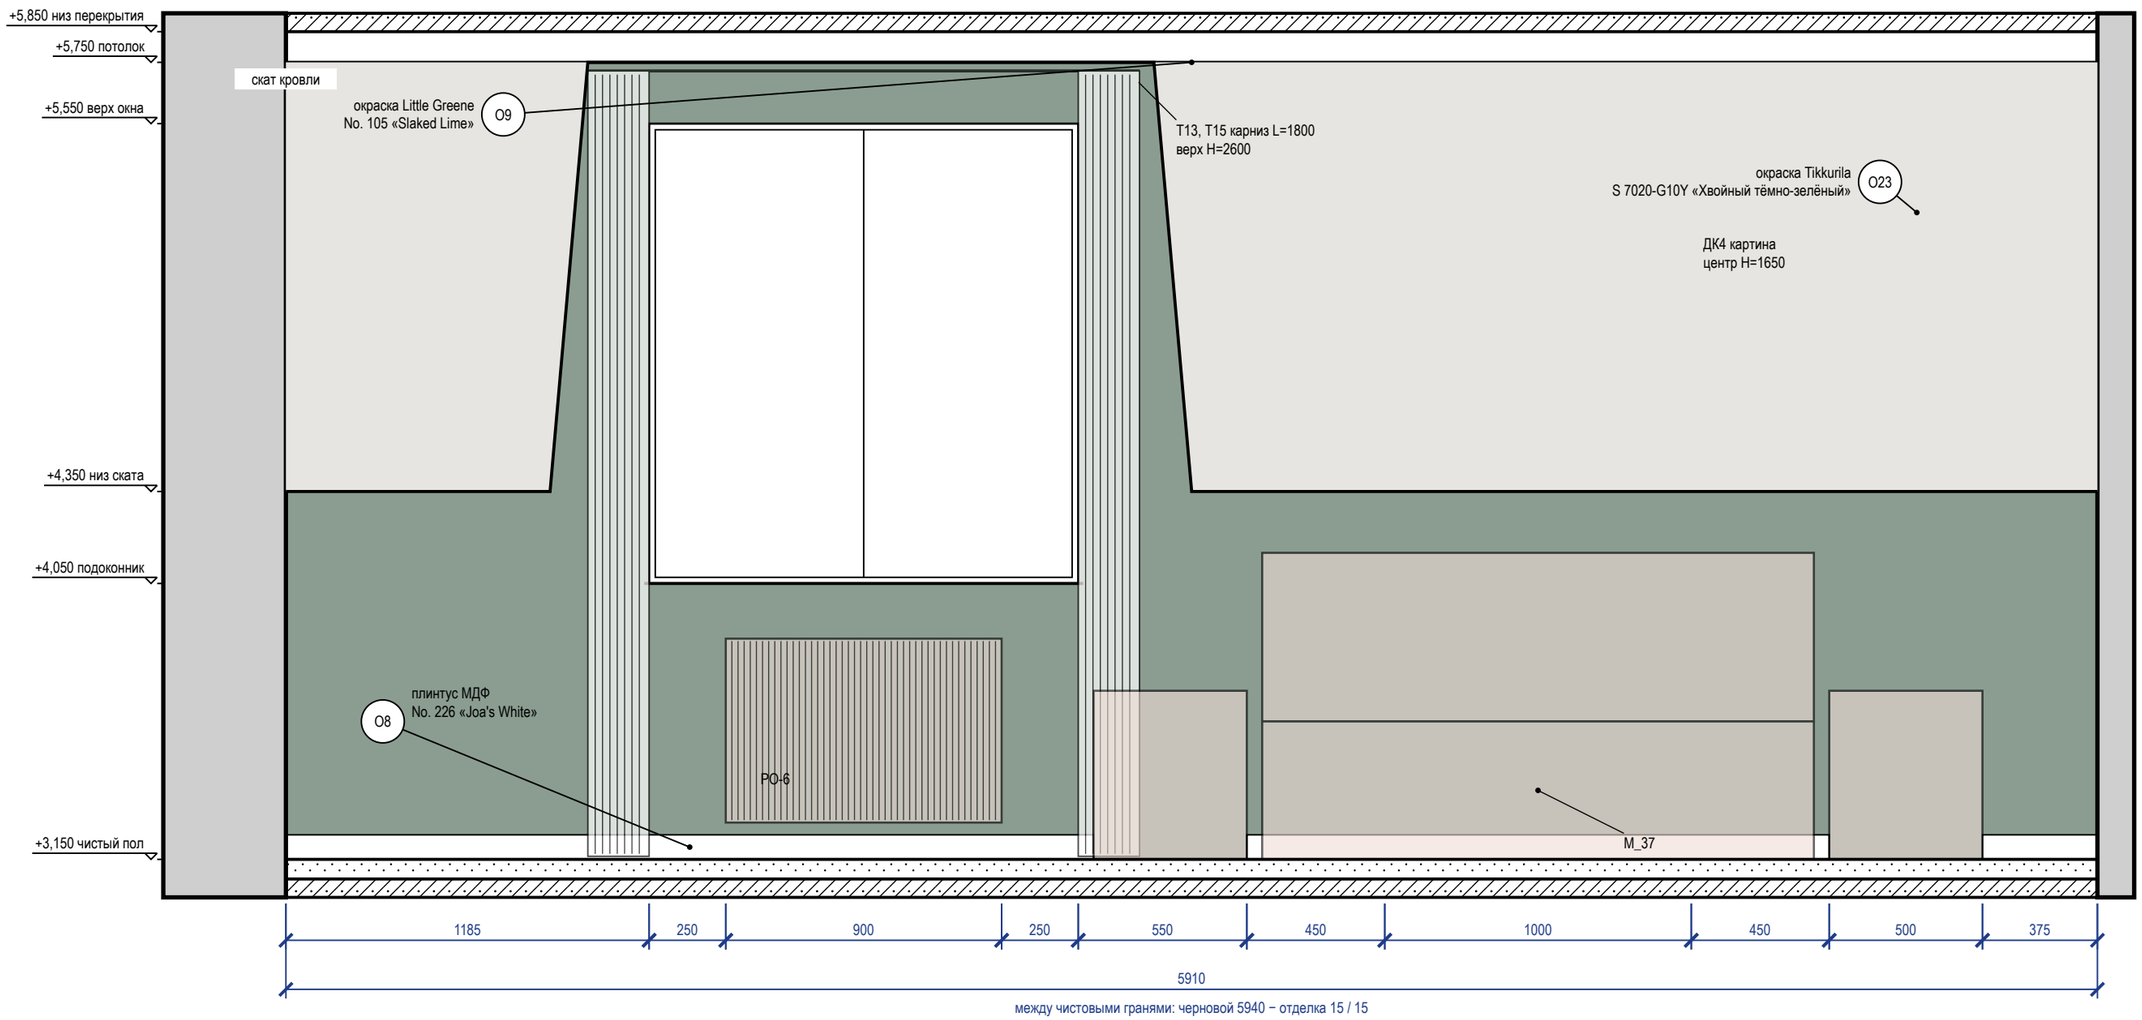


Схема развёрток (М 1:100)

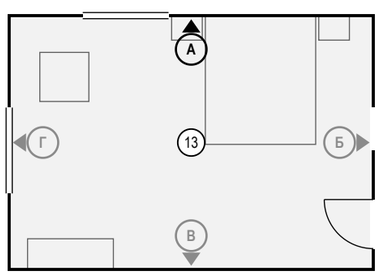

Ведомость отделки (на листе)

Марка	Поверхность	Материал, изделие	Цвет, код	Кол.
O8	плинтус	плинтус МДФ, h 80 мм, аналог: плинтус МДФ под покраску 80×16	Farrow & Ball No. 226 «Joa's White»	4,9 м
O9	потолок	окраска, Little Greene Absolute Matt, глубокоматовая, подготовка Q3	Little Greene No. 105 «Slaked Lime»	24,6 м²
O23	акцентная стена	окраска, Tikkurila Optiva 5 Matt, матовая, подготовка Q3	NCS S 7020-G10Y «Хвойный тёмно-зелёный»	13,3 м²

Примечания

1. Размеры — в мм от чистовых поверхностей стен; условные обозначения и общие указания — лист 3.
2. Стена А показана двумя видами: здесь — архитектурная развёртка (мебель, отделка, проёмы, высоты), электроточки и выводы ВК с привязками и таблицей — на листе 115 («Привязки»).
3. Картины и зеркала крепить к основанию по паспорту изделия (закладные и анкеры — в перечне скрытых работ); крест — ось центра предмета.
4. Карнизы (шины) — по ведомости текстиля декоратора: длина L и верх H на развёртке — те же числа, что в ведомости; крепление — до окраски потолка.
5. Потолок — у каждой стены свой, по плану потолков (ПТ6); ступени — зоной, кромка короба перед нишей — тонкой линией; в поле потолка: ПТ5 +5,650.

					Проект: Дом 331 м² — М 1:20
	Лист	№ док.	Подпись	Дата	Развёртка стены А. Спальня мастер (пом. 13)
Дизайнер	Кырлан А.С.			04.11.26	Стадия: П · Лист: 114 · Листов: 168

Развёртка стены А: электроточки и выводы

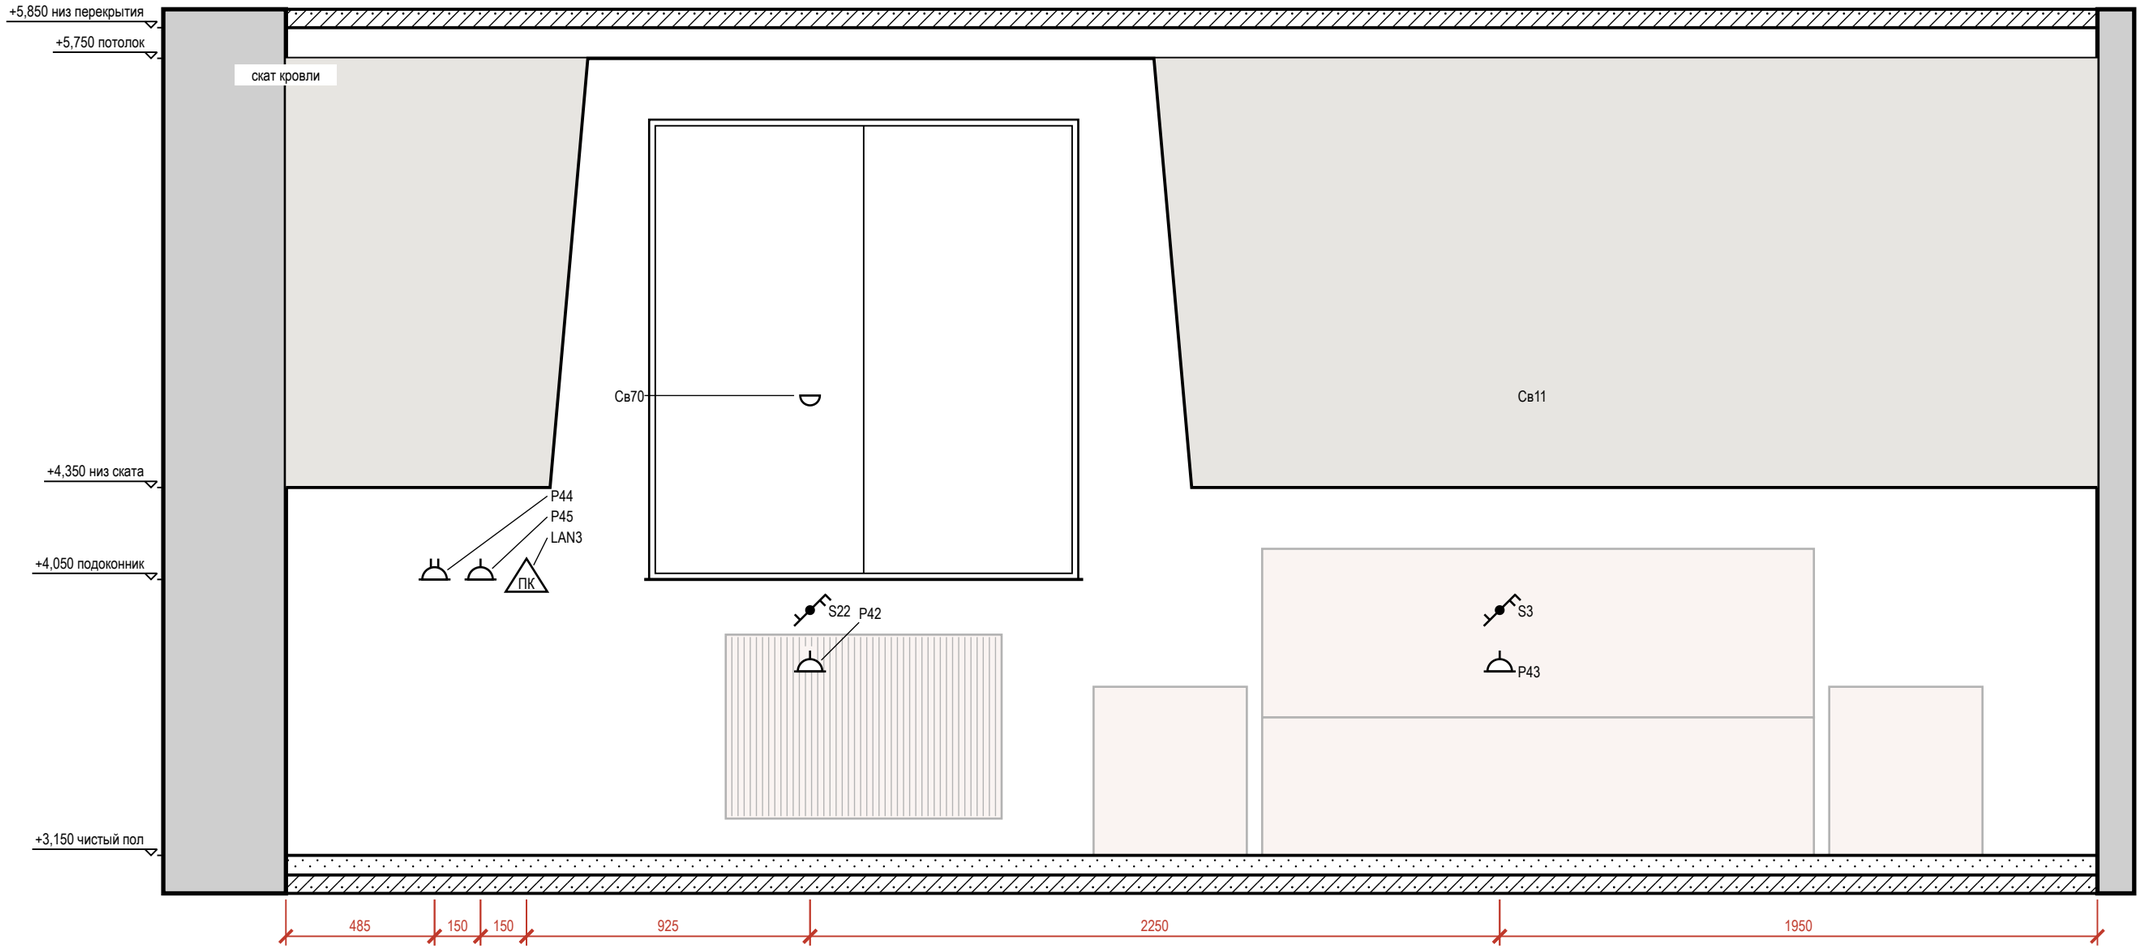



Таблица привязок электроточек и выводов

Марка	Назначение	От угла, мм	H от пола, мм	Примечание
P44	розетка: рабочий стол	485	900	рамка 2 поста, гр. 4
P45	розетка: рабочий стол	635	900	гр. 4
LAN3	розетка RJ45: рабочий стол	785	900	
P42	розетка: у кровати	1710	600	гр. 4
S22	выключатель	1710	800	гр. 1
Св70	светильник настенный	1710	1500	гр. 1
P43	розетка: у кровати	3960	600	гр. 4
S3	выключатель	3960	800	гр. 1
Св11	светильник настенный	3960	1500	гр. 1

Условные обозначения

- розетка с заземляющим контактом; у знака — марка, ×N постов в рамке, гр. — группа щита, H — высота оси, мм
- выключатель одноклавишный
- выключатель двухклавишный (флажков — по числу клавиш)
- выключатель с проходной или перекрёстной клавишей (обратный флажок); тип клавиши — в подписи
- светильник настенный (бра), H — высота оси
- ПК — розетка компьютерная RJ45
- привязки точек и выводов от угла и от пола, мм
- A — марка развёртки: буква стены, стрелка — взгляд

Схема развёрток (М 1:100)

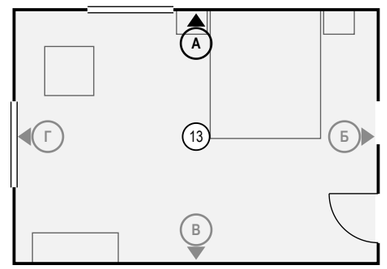

Примечания

1. Вид «Привязки» стены А — электроточки и выводы ВК; архитектурная развёртка (мебель, отделка, проёмы, высоты) — на листе 114. Мебель и приборы — подложкой для ориентира; их марки и обозначения мебели, проёмов и стен — там же.
2. Привязки — в мм: по горизонтали от левого чистового угла стены до оси изделия, H — от чистого пола до оси; все точки — в таблице привязок. Красная цепочка — привязки по осям; точки ближе 120 мм одна к другой в цепочку не дробятся — их привязки только в таблице.
3. У знака — марка электроточки (P — розетка, S — выключатель, Св — светильник, ЭВ — вывод кабеля); условные обозначения и общие указания — лист 3.
4. Линии узора (швы плитки, складки штор, рёбра радиаторов) прерываются у знаков и выносок — просвет между линиями не менее 0,7 мм.

					Проект: Дом 331 м² — М 1:20
	Лист	№ док.	Подпись	Дата	Привязки электроточек, стена А. Спальня мастер (пом. 13)
Дизайнер	Кырлан А.С.			04.11.26	Стадия: П; Лист: 115; Листов: 168

Развёртка стены Б


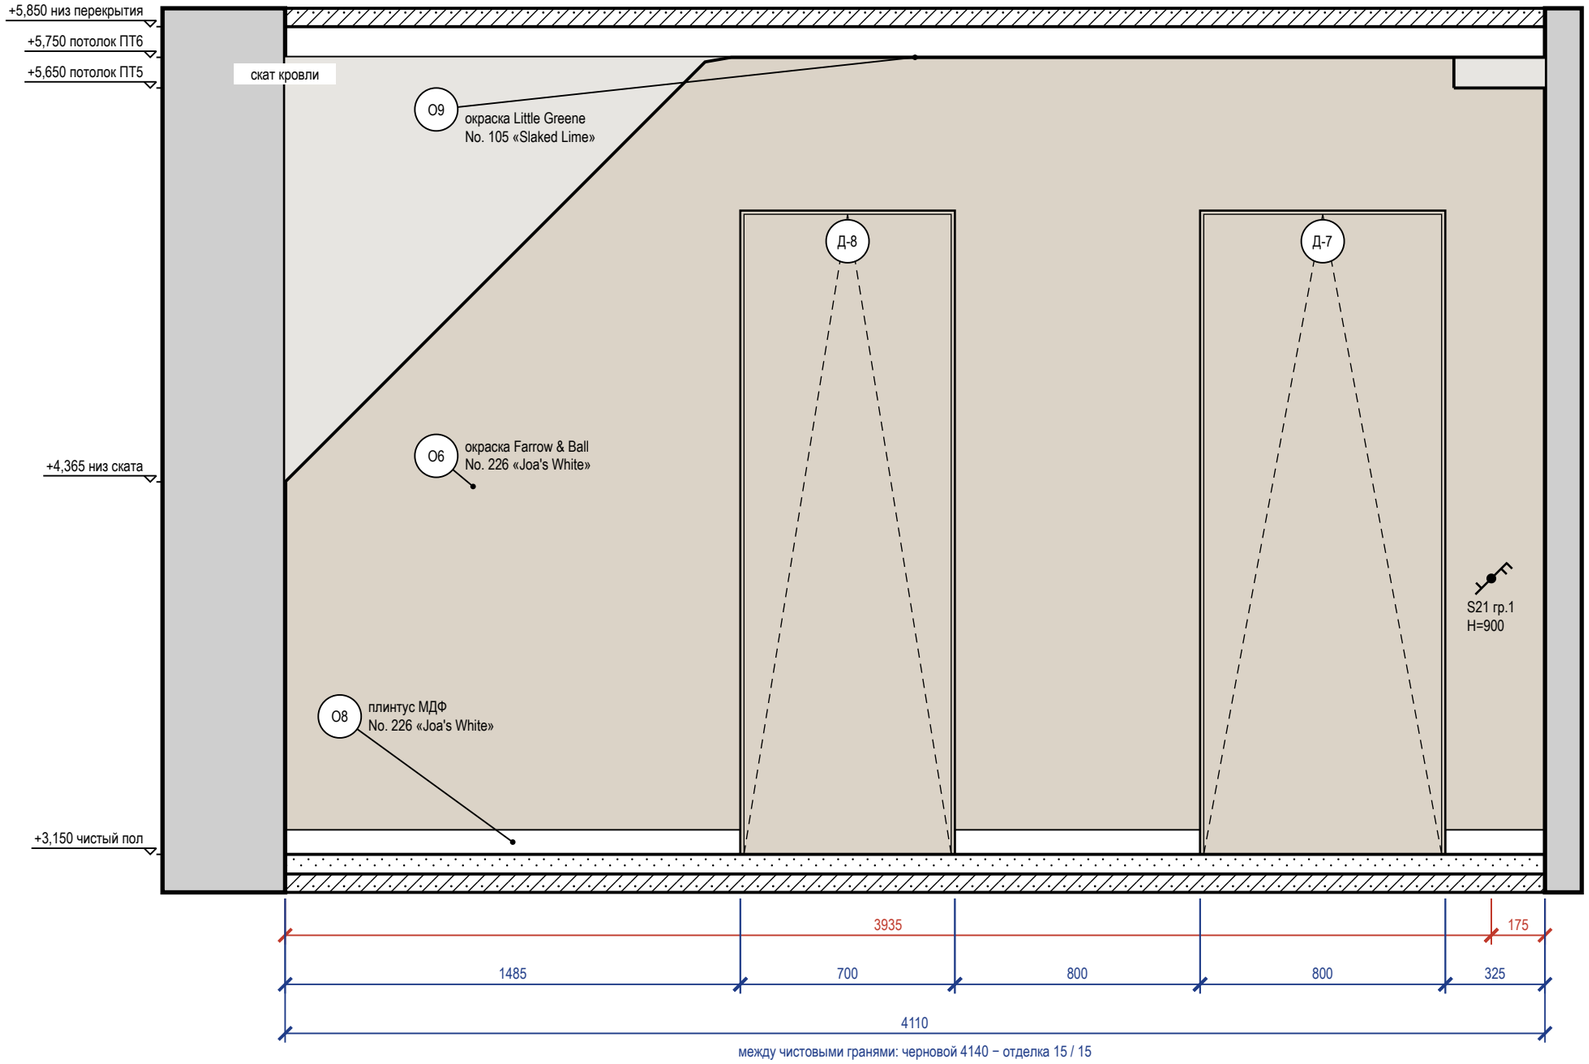


Схема развёрток (М 1:100)

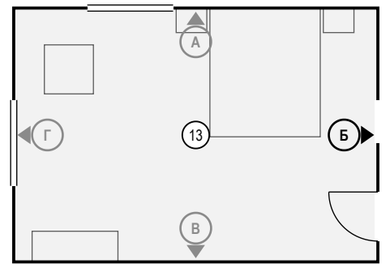

Ведомость отделки (на листе)


Марка	Поверхность	Материал, изделие	Цвет, код	Кол.
О6	стены	окраска, Farrow & Ball Modern Emulsion, матовая, подготовка Q3	Farrow & Ball No. 226 «Joa's White»	7,5 м²
О8	плинтус	плинтус МДФ, h 80 мм, аналог: плинтус МДФ под покраску 80×16	Farrow & Ball No. 226 «Joa's White»	2,6 м
О9	потолок	окраска, Little Greene Absolute Matt, глубокоматовая, подготовка Q3	Little Greene No. 105 «Slaked Lime»	24,6 м²

Примечания

1. Размеры — в мм от чистовых поверхностей стен; условные обозначения и общие указания — лист 3.
2. Двери скрытого монтажа — полотно в плоскости стены, отделка стены по полотну, плинтус прерывается у короба (узел — на листе узлов).
3. Потолок — у каждой стены свой, по плану потолков (ПТ6, ПТ5); ступени — зоной, кромка короба перед нишей — тонкой линией.


					Проект: Дом 331 м²	М 1:20
	Лист	№ док.	Подпись	Дата		
Дизайнер	Кырлан А.С.			04.11.26	Развёртка стены Б. Спальня мастер (пом. 13)	Стадия: П; Лист: 116; Листов: 168

Развёртка стены В

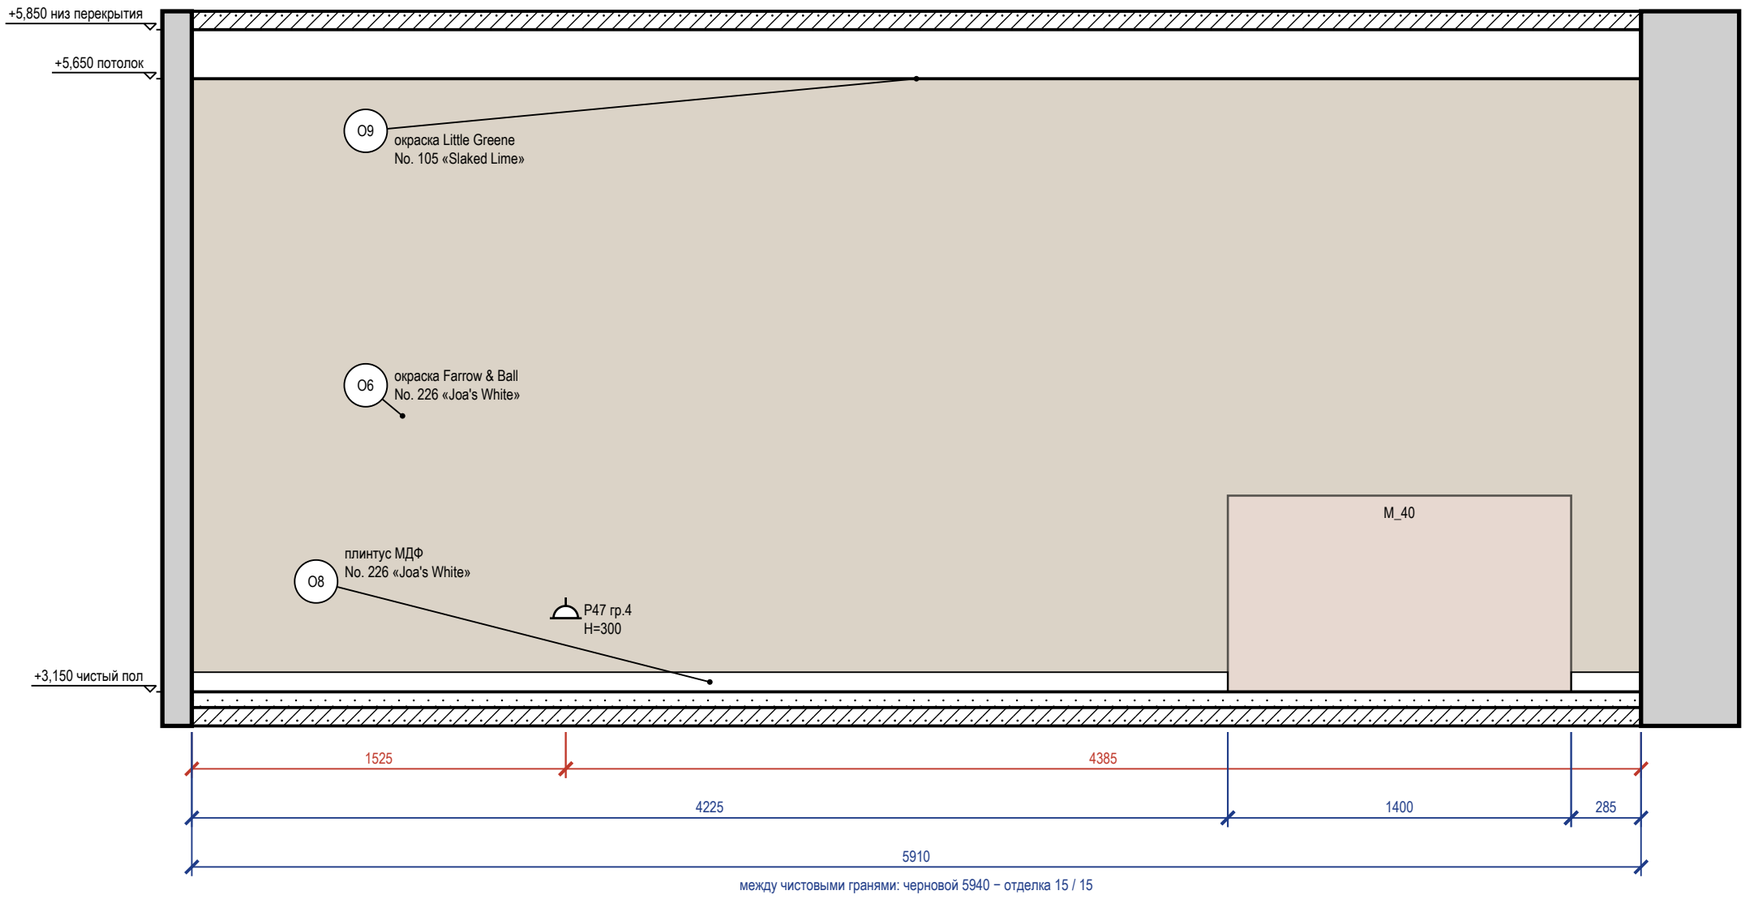

между чистовыми гранями: черновой 5940 − отделка 15 / 15

Схема развёрток (М 1:100)

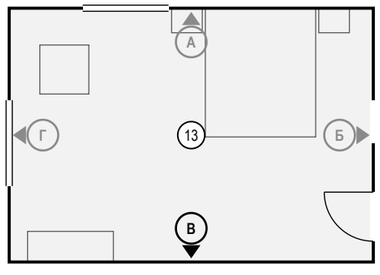

Ведомость отделки (на листе)

Марка	Поверхность	Материал, изделие	Цвет, код	Кол.
О6	стены	окраска, Farrow & Ball Modern Emulsion, матовая, подготовка Q3	Farrow & Ball No. 226 «Joa's White»	14,8 м²
О8	плинтус	плинтус МДФ, h 80 мм, аналог: плинтус МДФ под покраску 80×16	Farrow & Ball No. 226 «Joa's White»	4,5 м
О9	потолок	окраска, Little Greene Absolute Matt, глубокоматовая, подготовка Q3	Little Greene No. 105 «Slaked Lime»	24,6 м²

Примечания

1. Размеры — в мм от чистовых поверхностей стен; условные обозначения и общие указания — лист 3.
2. Потолок — у каждой стены свой, по плану потолков (ПТ5); ступени — зоной, кромка короба перед нишей — тонкой линией; в поле потолка: ПТ6 +5,750.

					Проект: Дом 331 м²	М 1:25
	Лист	№ док.	Подпись	Дата	Развёртка стены В. Спальня мастер (пом. 13)	Стадия / Лист / Листов
Дизайнер	Кырлан А.С.			04.11.26		П / 117 / 168

выпуск 04.11.2026 № f163a372b2 · стр. 117 из 168

Развёртка стены Г


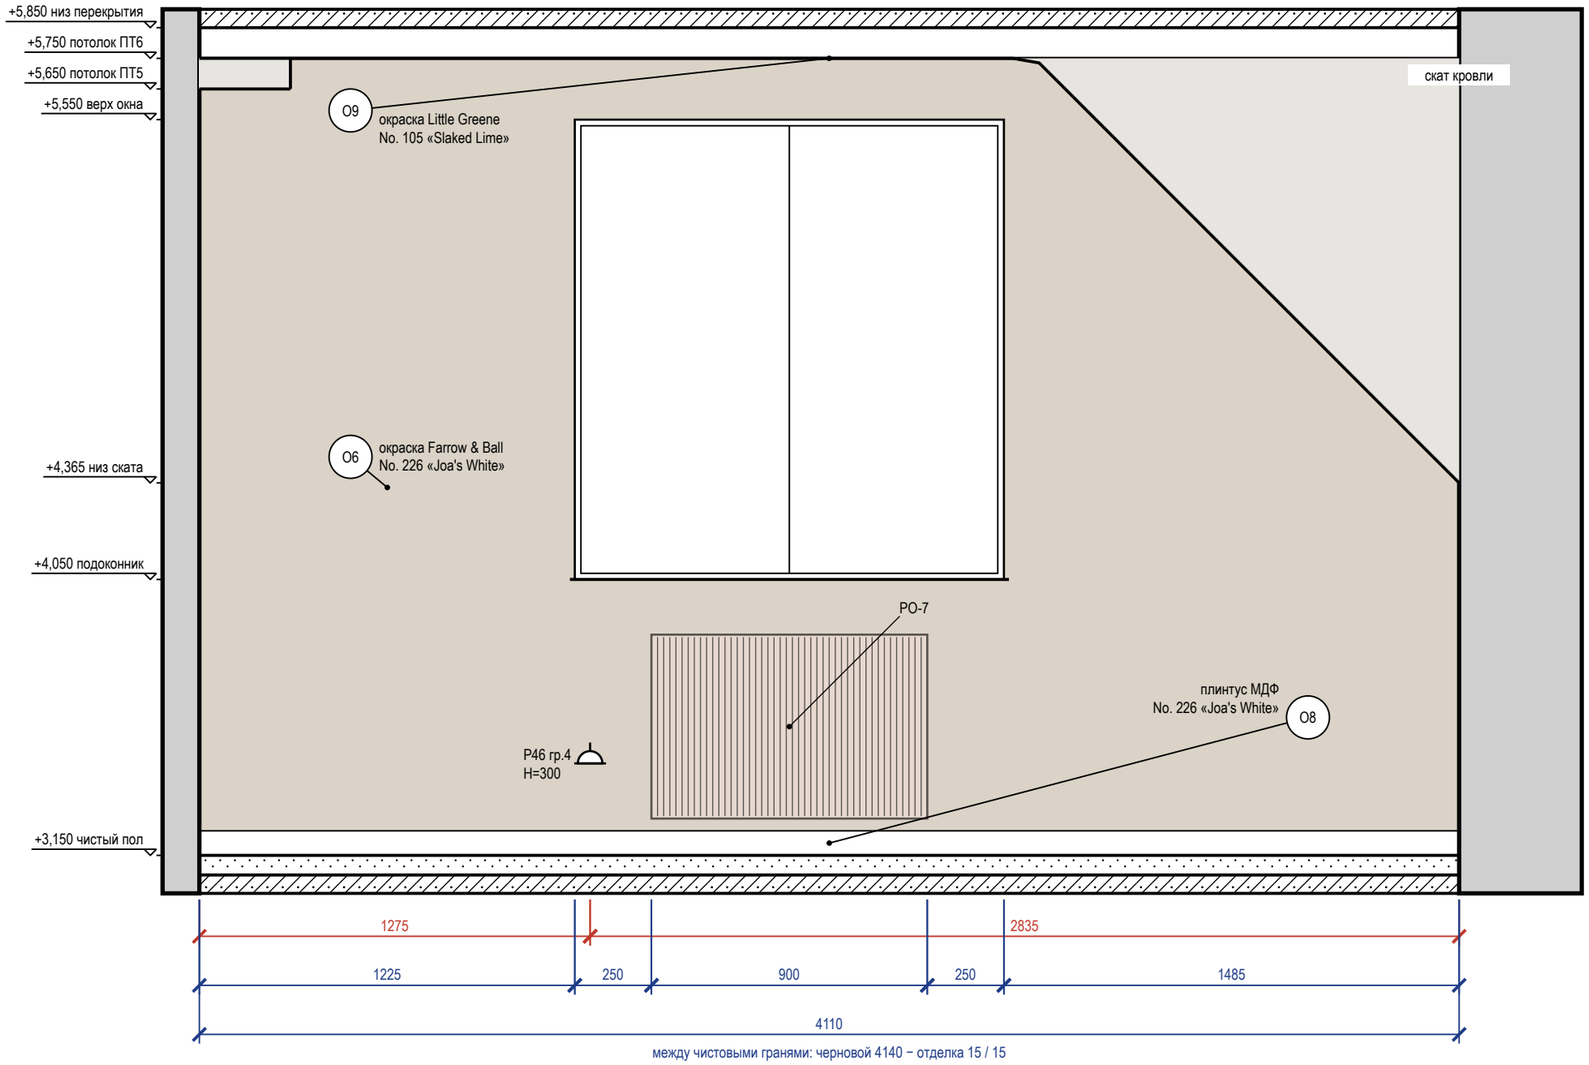


Схема развёрток (М 1:100)

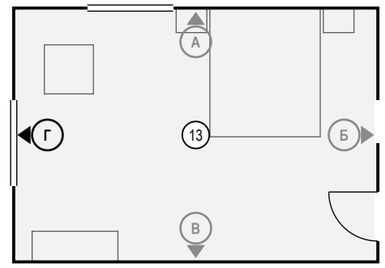

Ведомость отделки (на листе)

Марка	Поверхность	Материал, изделие	Цвет, код	Кол.
О6	стены	окраска, Farrow & Ball Modern Emulsion, матовая, подготовка Q3	Farrow & Ball No. 226 «Joa's White»	8,6 м²
О8	плинтус	плинтус МДФ, h 80 мм, аналог: плинтус МДФ под покраску 80×16	Farrow & Ball No. 226 «Joa's White»	4,1 м
О9	потолок	окраска, Little Greene Absolute Matt, глубокоматовая, подготовка Q3	Little Greene No. 105 «Slaked Lime»	24,6 м²


Примечания

1. Размеры — в мм от чистовых поверхностей стен; условные обозначения и общие указания — лист 3.
2. Потолок — у каждой стены свой, по плану потолков (ПТ6, ПТ5); ступени — зоной, кромка короба перед нишей — тонкой линией.

					Проект: Дом 331 м² — М 1:20
	Лист	№ док.	Подпись	Дата	Развёртка стены Г. Спальня мастер (пом. 13)
Дизайнер	Кырлан А.С.			04.11.26	


Стадия	Лист	Листов
П	118	168

Развёртка стены А

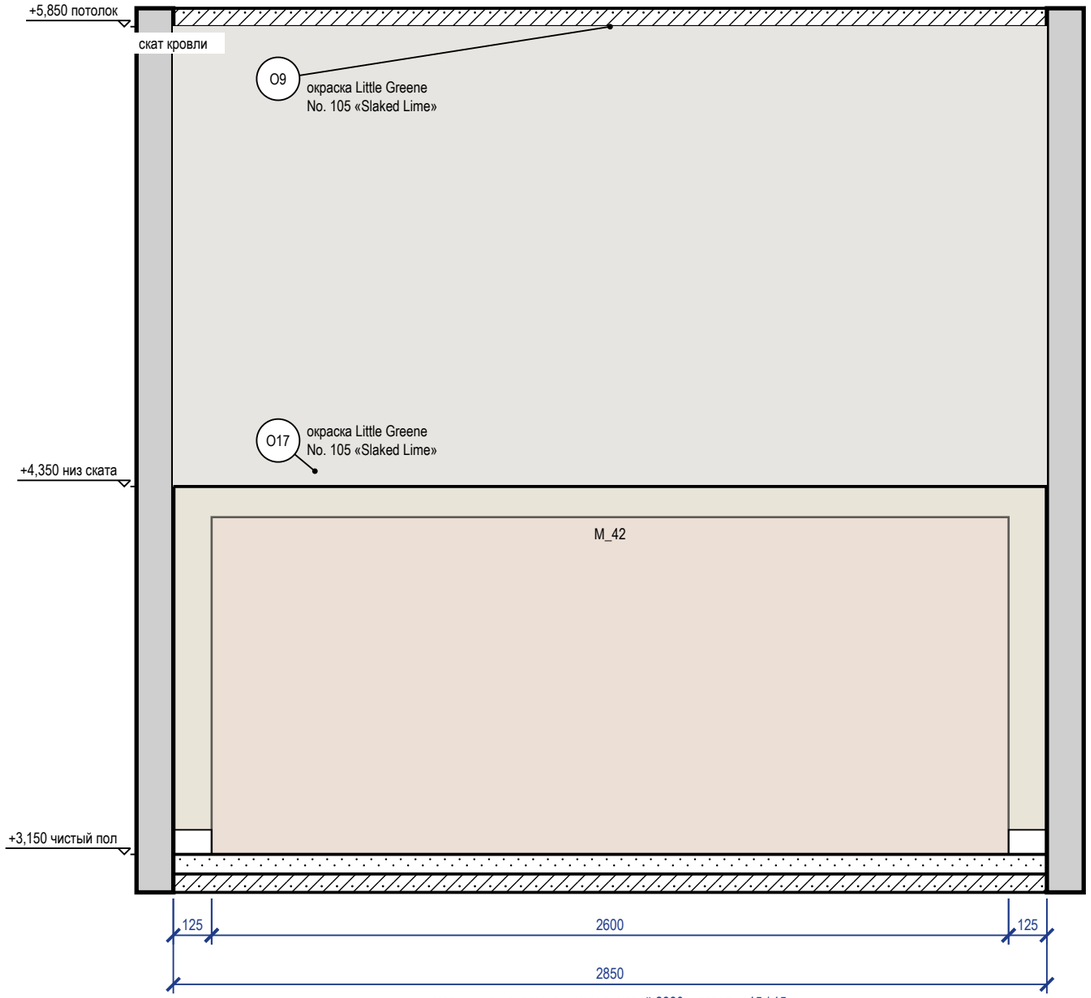


между чистовыми гранями: черновой 2880 − отделка 15 / 15

Развёртка стены Б

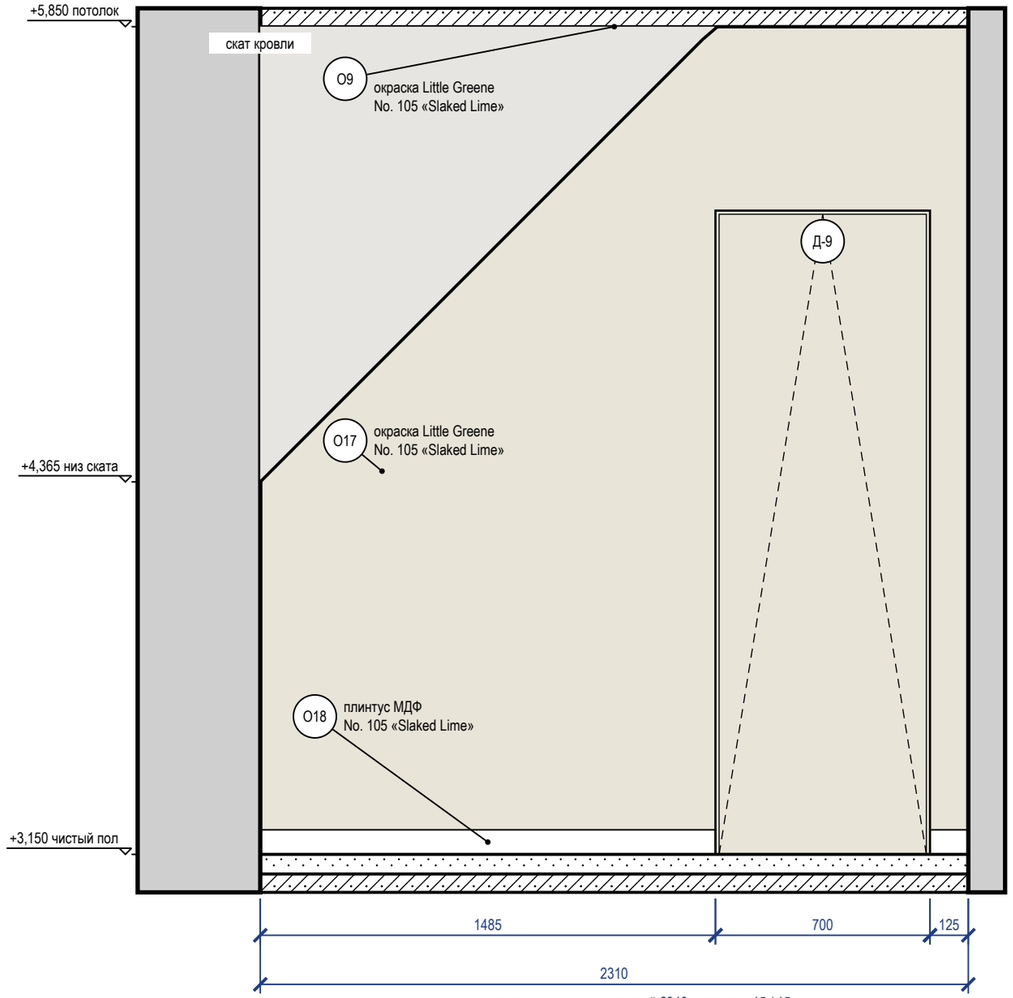

между чистовыми гранями: черновой 2340 − отделка 15 / 15

Схема развёрток (М 1:100)

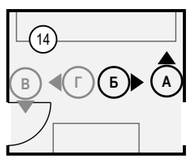

Ведомость отделки (на листе)


Марка	Поверхность	Материал, изделие	Цвет, код	Кол.
О9	потолок	окраска, Little Greene Absolute Matt, глубокоматовая, подготовка Q3	Little Greene No. 105 «Slaked Lime»	6,7 м²
О17	стены	окраска, Little Greene Intelligent Matt, матовая, подготовка Q3	Little Greene No. 105 «Slaked Lime»	12,5 м²
О18	плинтус	плинтус МДФ, h 80 мм, аналог: плинтус МДФ под покраску 80×16	Little Greene No. 105 «Slaked Lime»	1,9 м

Примечания

1. Размеры — в мм от чистовых поверхностей стен; условные обозначения и общие указания — лист 3.
2. Двери скрытого монтажа — полотно в плоскости стены, отделка стены по полотну, плинтус прерывается у короба (узел — на листе узлов).


					Проект: Дом 331 м²	М 1:20
	Лист	№ док.	Подпись	Дата	Развёртки стен А, Б. Гардеробная мастер (пом. 14)	Стадия / Лист / Листов
Дизайнер	Кырлан А.С.			04.11.26		П / 119 / 168

Развёртка стены В

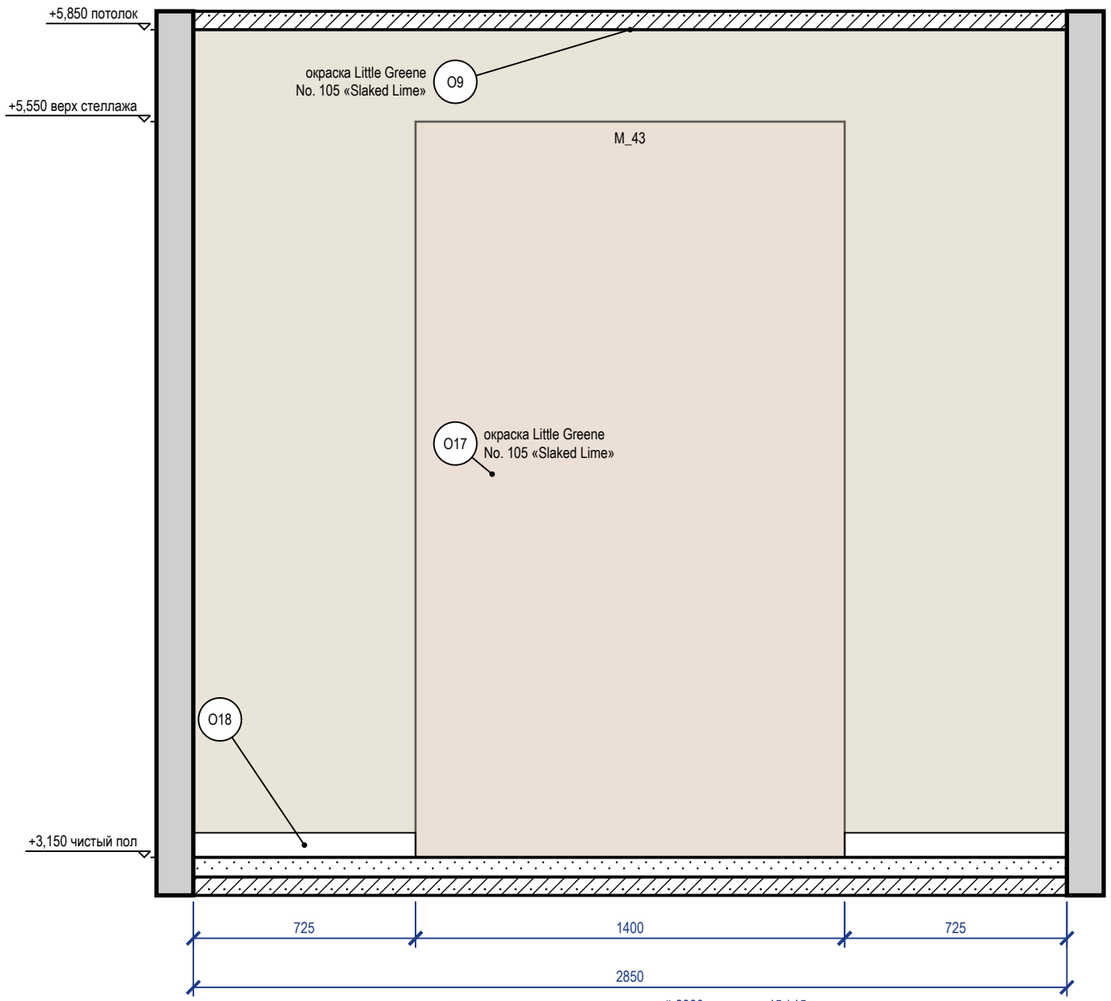


между чистовыми гранями: черновой 2880 − отделка 15 / 15

Развёртка стены Г

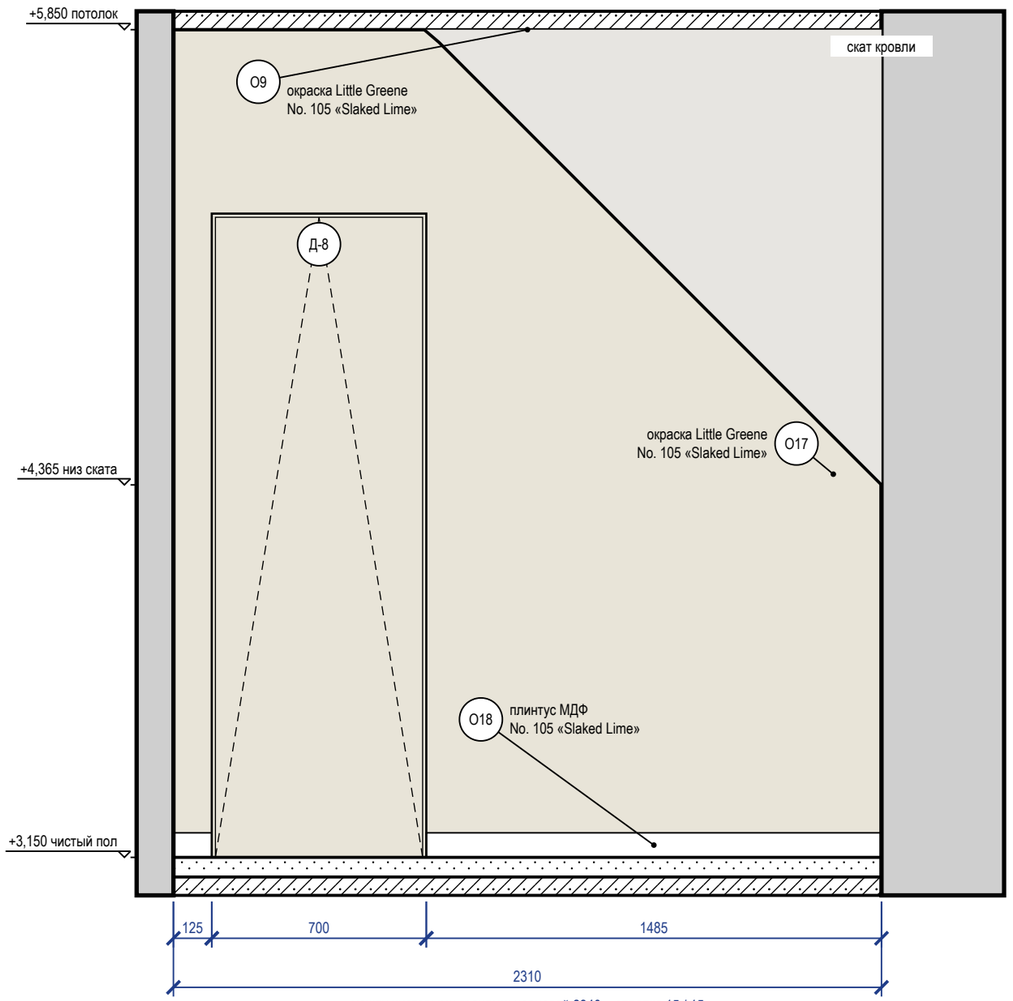

между чистовыми гранями: черновой 2340 − отделка 15 / 15

Схема развёрток (М 1:100)

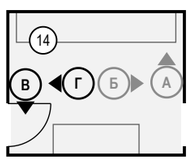

Ведомость отделки (на листе)

Марка	Поверхность	Материал, изделие	Цвет, код	Кол.
О9	потолок	окраска, Little Greene Absolute Matt, глубокоматовая, подготовка Q3	Little Greene No. 105 «Slaked Lime»	6,7 м²
О17	стены	окраска, Little Greene Intelligent Matt, матовая, подготовка Q3	Little Greene No. 105 «Slaked Lime»	12,5 м²
О18	плинтус	плинтус МДФ, h 80 мм, аналог: плинтус МДФ под покраску 80×16	Little Greene No. 105 «Slaked Lime»	3,1 м

Примечания

1. Размеры — в мм от чистовых поверхностей стен; условные обозначения и общие указания — лист 3.
2. Двери скрытого монтажа — полотно в плоскости стены, отделка стены по полотну, плинтус прерывается у короба (узел — на листе узлов).


	Лист	№ док.	Подпись	Дата
Дизайнер	Кырлан А.С.			04.11.26

Проект: Дом 331 м² — М 1:20

Развёртки стен В, Г. Гардеробная мастер (пом. 14)


Стадия	Лист	Листов
П	120	168

Развёртка стены А

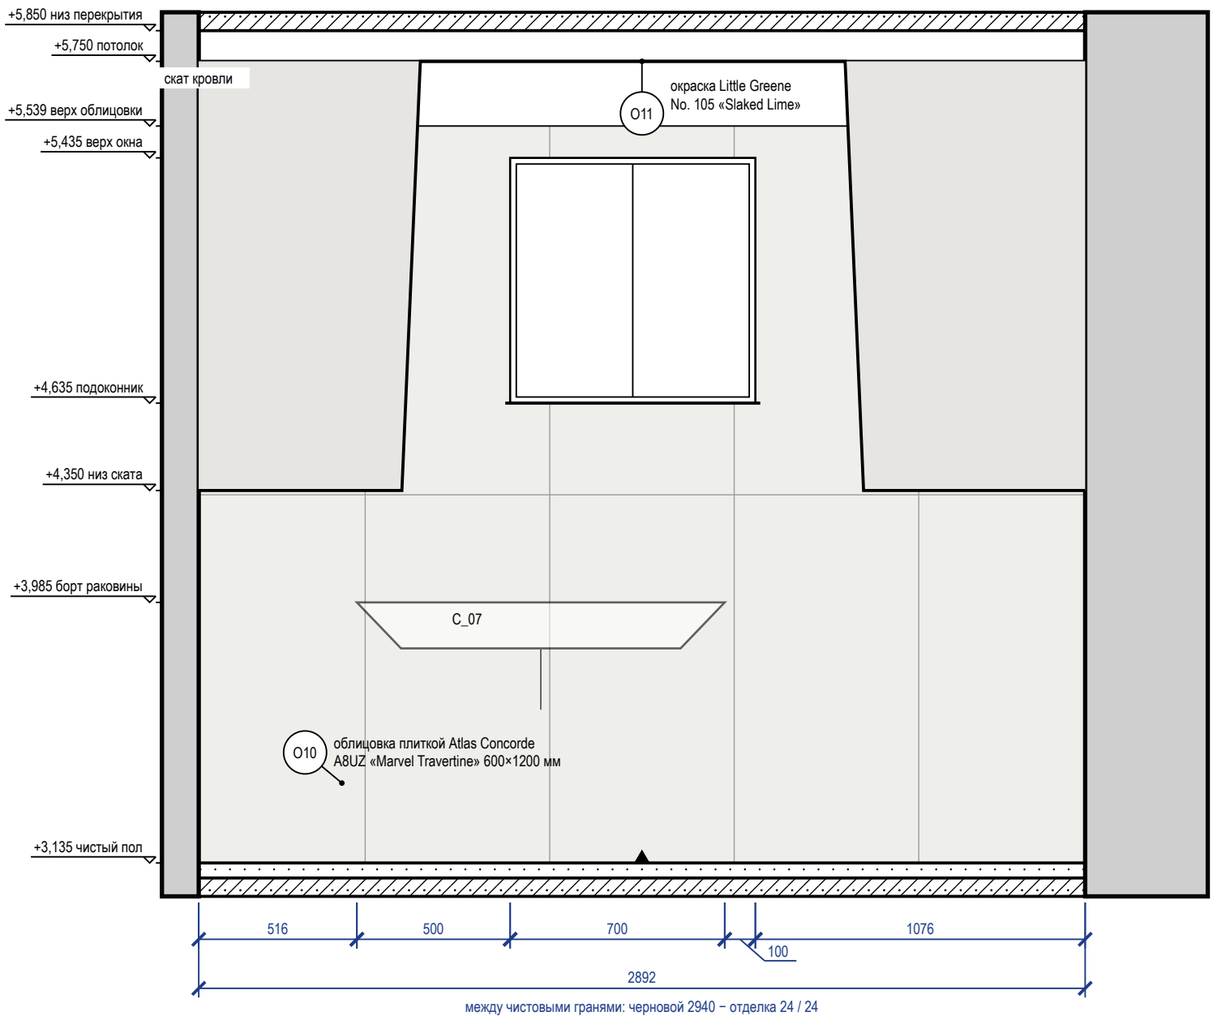


между чистовыми гранями: черновой 2940 − отделка 24 / 24

Развёртка стены Б

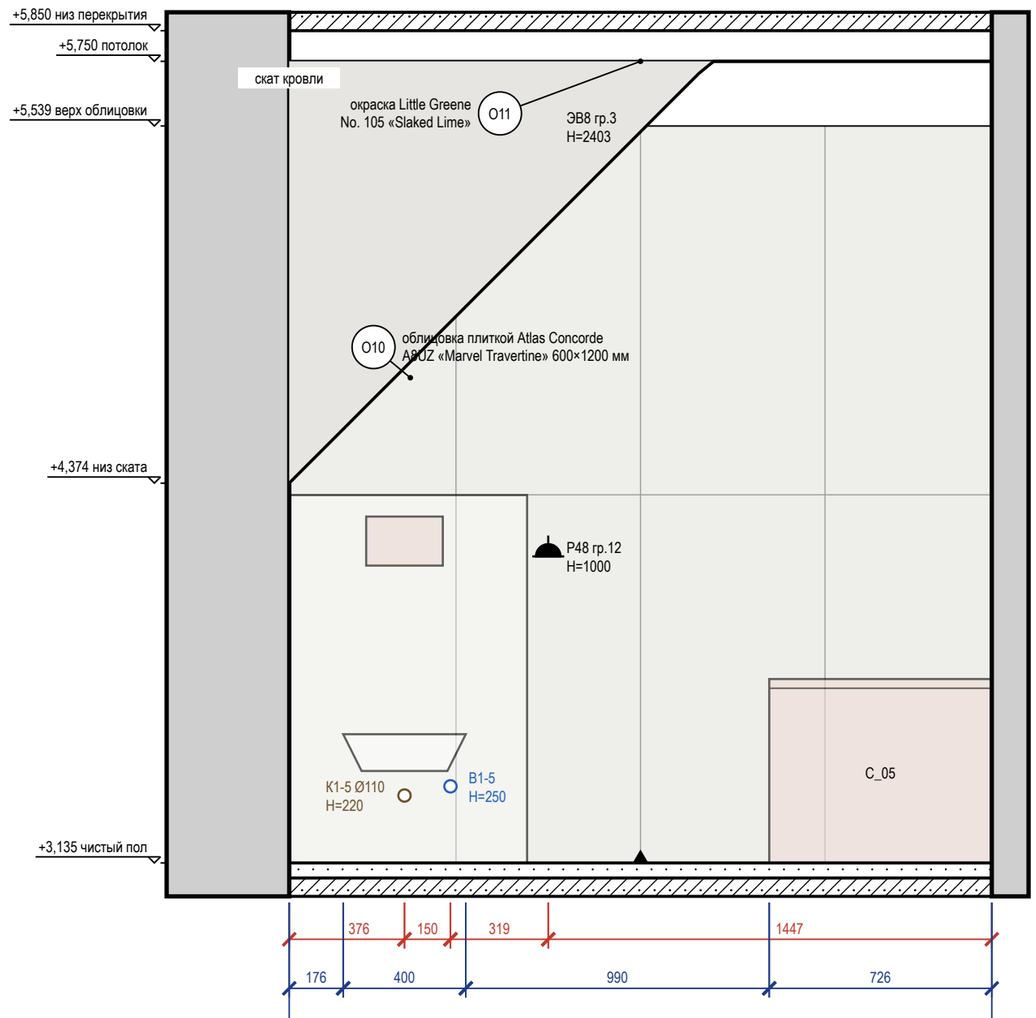

между чистовыми гранями: черновой 2340 − отделка 24 / 24

Схема развёрток (М 1:100)

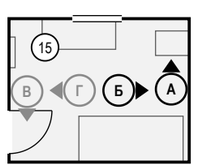

Ведомость отделки (на листе)


Марка	Поверхность	Материал, изделие	Цвет, код	Кол.
О10	стены	облицовка плиткой, Atlas Concorde Marvel Travertine, 600×1200×9 мм, A8UZ, затирка CG2WA	Atlas Concorde A8UZ «Marvel Travertine»	11,8 м²
О11	потолок	окраска, Little Greene Intelligent Bathroom, матовая, подготовка Q3	Little Greene No. 105 «Slaked Lime»	6,9 м²

Примечания

1. Размеры — в мм от чистовых поверхностей стен; условные обозначения и общие указания — лист 3.
2. Стена А показана двумя видами: здесь — архитектурная развёртка (мебель, отделка, проёмы, высоты), электроточки и выводы ВК с привязками и таблицей — на листе 123 («Привязки»).
3. Схема мебели, приборов и декора не является технической документацией для производства мебели; габариты — по паспортам изделий.
4. Выводы ВК — коды и высоты по листу выводов сантехники.
5. Облицовка — по сетке швов 2 мм, раскладка от оси стены (треугольник у пола), целые ряды от пола; подрезки — по листу раскладки плитки.
6. Гидроизоляция в 2 слоя, заход на стены 200 мм; над ванной — до 2000 и 300 мм за борт — до облицовки, с актом скрытых работ и тестом проливом (узел — на листе узлов).

					Проект: Дом 331 м²	М 1:20
	Лист	№ док.	Подпись	Дата		
Дизайнер	Кырлан А.С.			04.11.26	Развёртки стен А, Б. Санузел мастер (пом. 15)	Стадия: П; Лист: 121; Листов: 168

Развёртка стены В

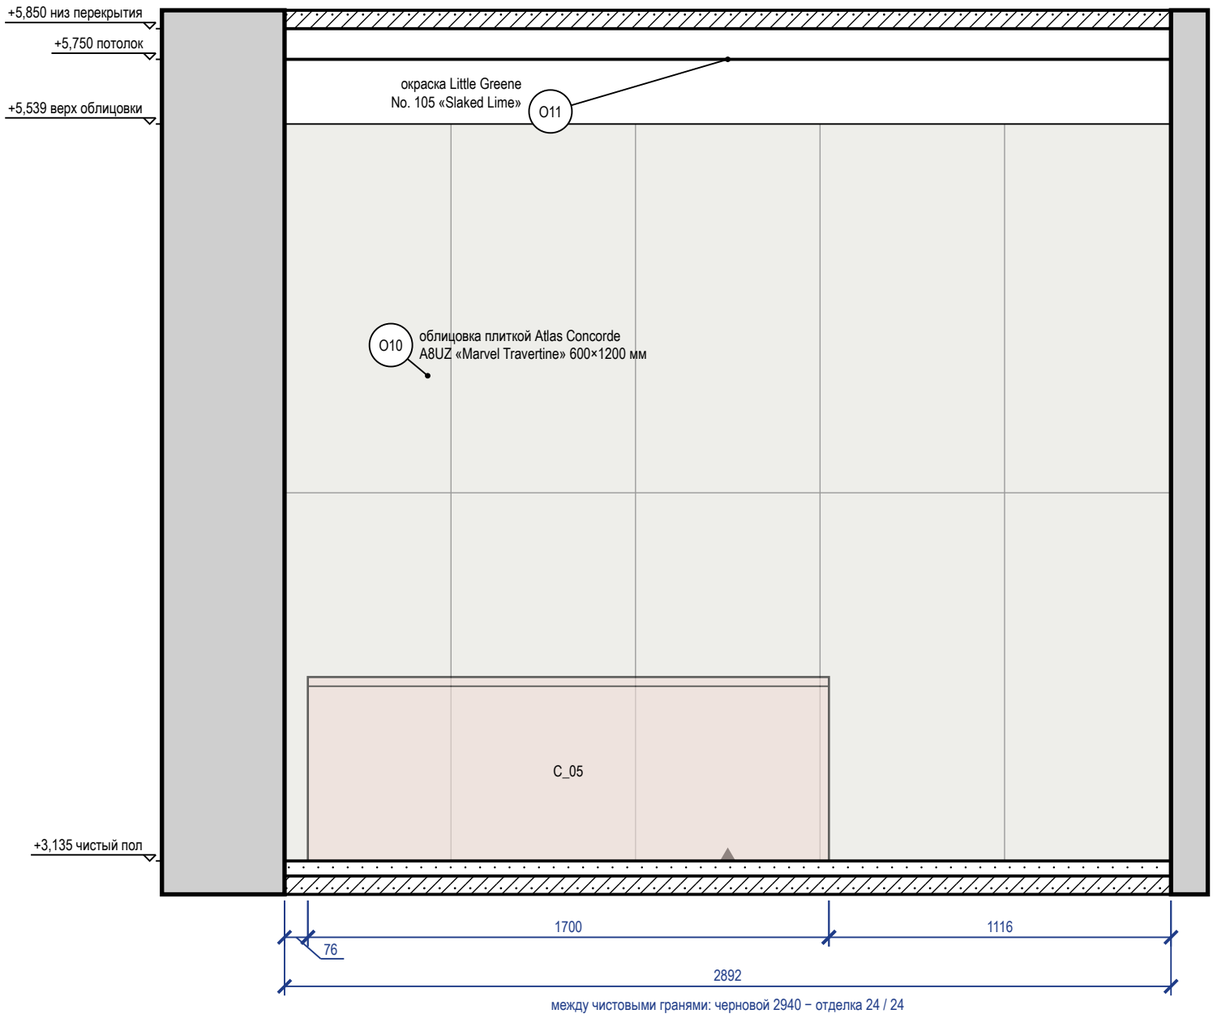

Развёртка стены Г


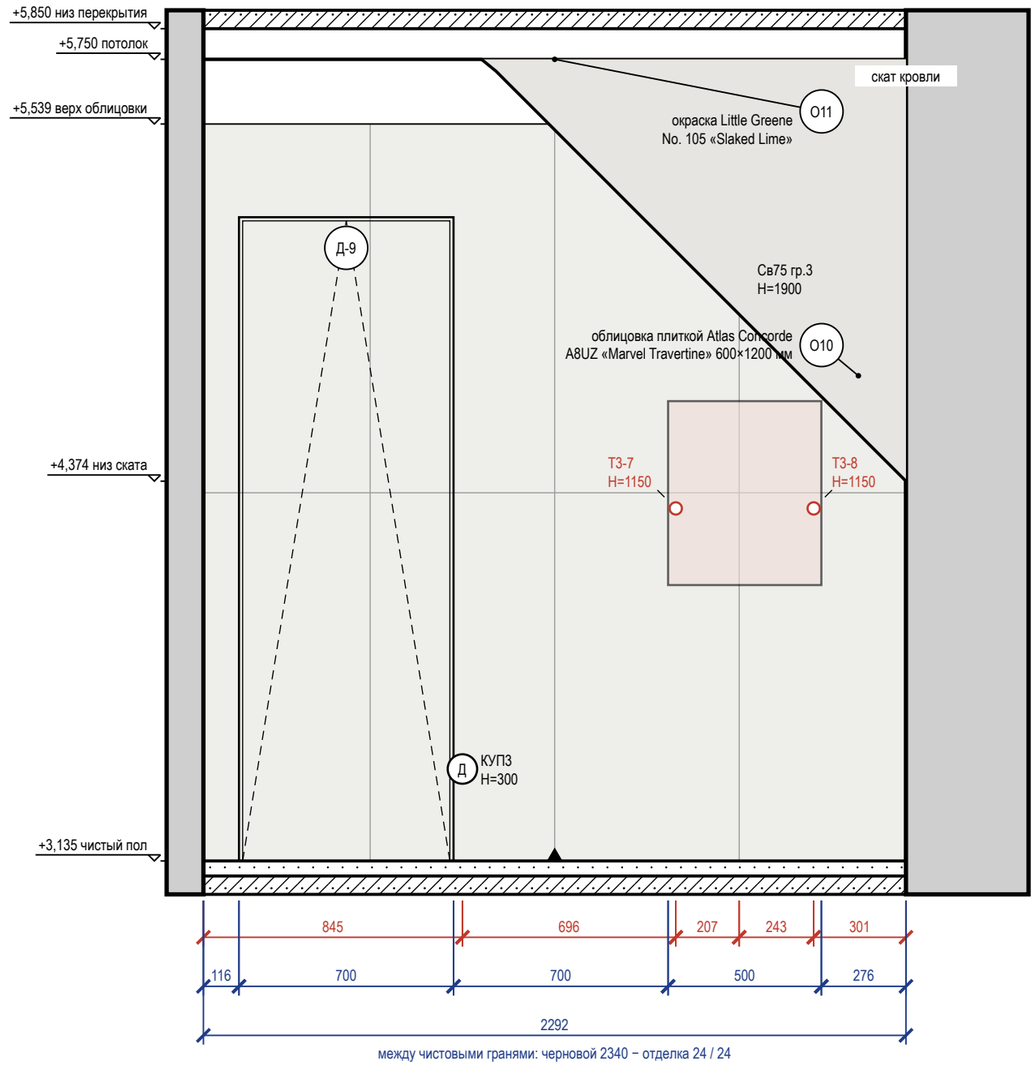


Схема развёрток (М 1:100)

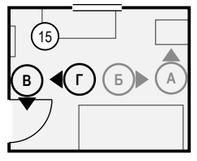

Ведомость отделки (на листе)

Марка	Поверхность	Материал, изделие	Цвет, код	Кол.
О10	стены	облицовка плиткой, Atlas Concorde Marvel Travertine, 600×1200×9 мм, A8UZ, затирка CG2WA	Atlas Concorde A8UZ «Marvel Travertine»	11 м²
О11	потолок	окраска, Little Greene Intelligent Bathroom, матовая, подготовка Q3	Little Greene No. 105 «Slaked Lime»	6,9 м²


Примечания

1. Размеры — в мм от чистовых поверхностей стен; условные обозначения и общие указания — лист 3.
2. Стена В показана двумя видами: здесь — архитектурная развёртка (мебель, отделка, проёмы, высоты), электроточки и выводы ВК с привязками и таблицей — на листе 123 («Привязки»).
3. Схема мебели, приборов и декора не является технической документацией для производства мебели; габариты — по паспортам изделий.
4. Выводы ВК — коды и высоты по листу выводов сантехники.
5. Облицовка — по сетке швов 2 мм, раскладка от оси стены (треугольник у пола), целые ряды от пола; подрезки — по листу раскладки плитки.
6. Гидроизоляция в 2 слоя, заход на стены 200 мм; над ванной — до 2000 и 300 мм за борт — до облицовки, с актом скрытых работ и тестом проливом (узел — на листе узлов).
7. Двери скрытого монтажа — полотно в плоскости стены, отделка стены по полотну, плинтус прерывается у короба (узел — на листе узлов).

					Проект: Дом 331 м² — М 1:20
	Лист	№ док.	Подпись	Дата	
Дизайнер	Кырлан А.С.			04.11.26	Развёртки стен В, Г. Санузел мастер (пом. 15)
					Стадия: П; Лист: 122; Листов: 168

выпуск 04.11.2026 · f163a372b2 · стр. 122 из 168

Развёртка стены А: электроточки и выводы

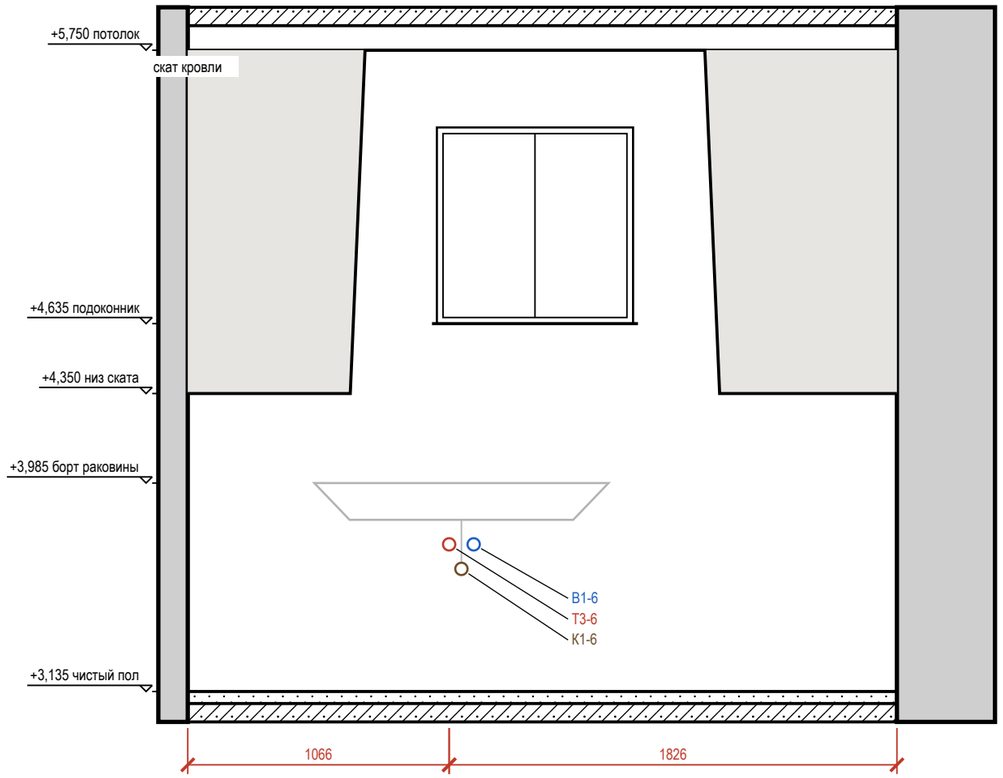

Развёртка стены В: электроточки и выводы

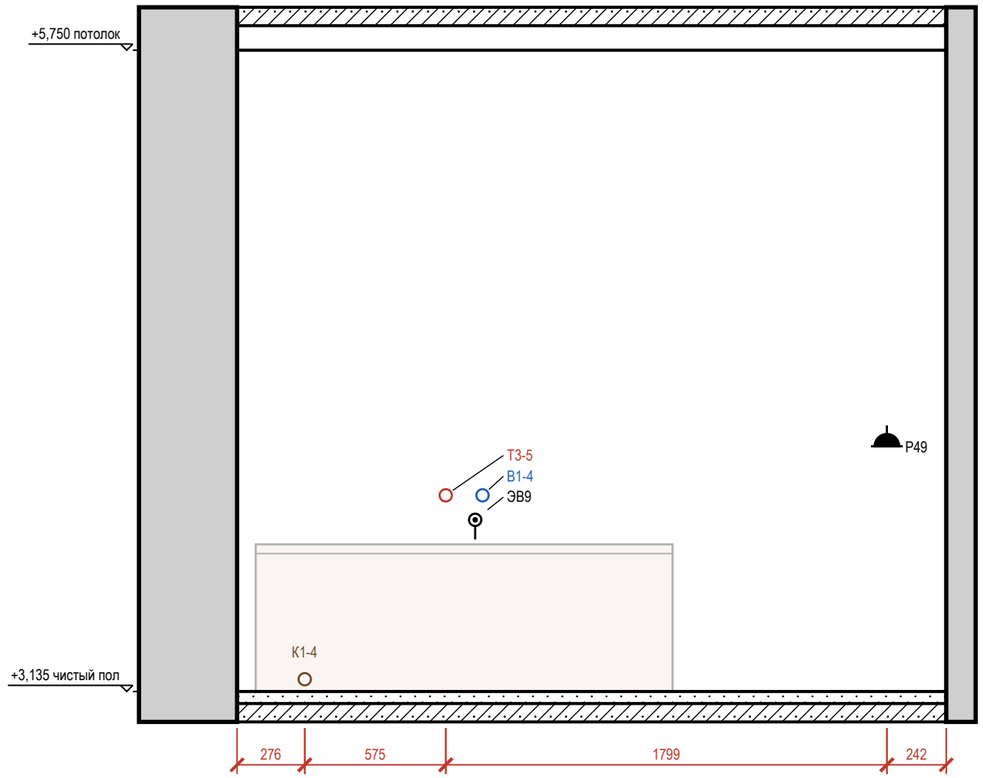



Таблица привязок электроточек и выводов

Стена	Марка	Назначение	От угла, мм	H от пола, мм	Примечание
A	T3-6	горячая вода — умывальник	1066	600	межос. 100
A	K1-6	канализация — умывальник	1116	500	Ø50
A	B1-6	холодная вода — умывальник	1166	600	межос. 100
B	K1-4	канализация — ванна	276	50	Ø50
B	T3-5	горячая вода — ванна	851	800	межос. 150
B	ЭВ9	вывод кабеля: полотенцесушитель П10	971	700	гр. 13
B	B1-4	холодная вода — ванна	1001	800	межос. 150
B	P49	розетка: фен у умывальника	2650	1000	гр. 13, IP44

Условные обозначения

- розетка влагозащищённая IP44
- вывод кабеля для подключения прибора (без розетки), марка ЭВ
- вывод B1 (код — в ведомости привязок)
- вывод T3 (код — в ведомости привязок)
- вывод K1 (код — в ведомости привязок)
- привязки точек и выводов от угла и от пола, мм
- A — марка развёртки: буква стены, стрелка — взгляд

Схема развёрток (М 1:50)

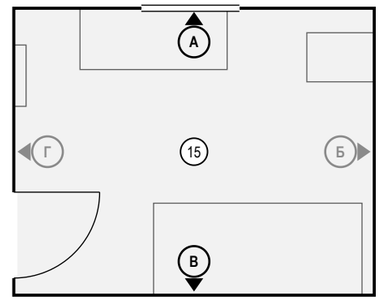

Примечания

1. Вид «Привязки» стен А, В — электроточки и выводы ВК; архитектурная развёртка (мебель, отделка, проёмы, высоты) — на листах 121, 122. Мебель и приборы подложкой для ориентира; их марки и обозначения мебели, проёмов и стен — там же.
2. Привязки — в мм: по горизонтали от левого чистового угла стены до оси изделия, H — от чистого пола до оси; все точки — в таблице привязок. Красная цепочка — привязки по осям; точки ближе 150 мм одна к другой в цепочку не дробятся — их привязки только в таблице.
3. У знака — марка электроточки (P — розетка, S — выключатель, Св — светильник, ЭВ — вывод кабеля); условные обозначения и общие указания — лист 3.
4. Коды выводов ВК: B1 — холодная вода, T3 — горячая вода, K1 — канализация; номер после дефиса — номер вывода на листе выводов сантехники.

					Проект: Дом 331 м² — М 1:25
	Лист	№ док.	Подпись	Дата	Привязки электроточек и выводов ВК, стены А, В. Санузел мастер (пом. 15)
Дизайнер	Кырлан А.С.			04.11.26	

Стадия	Лист	Листов
П	123	168

выпуск 04.11.2026 № f163a372b2 · стр. 123 из 168

Развёртка стены А


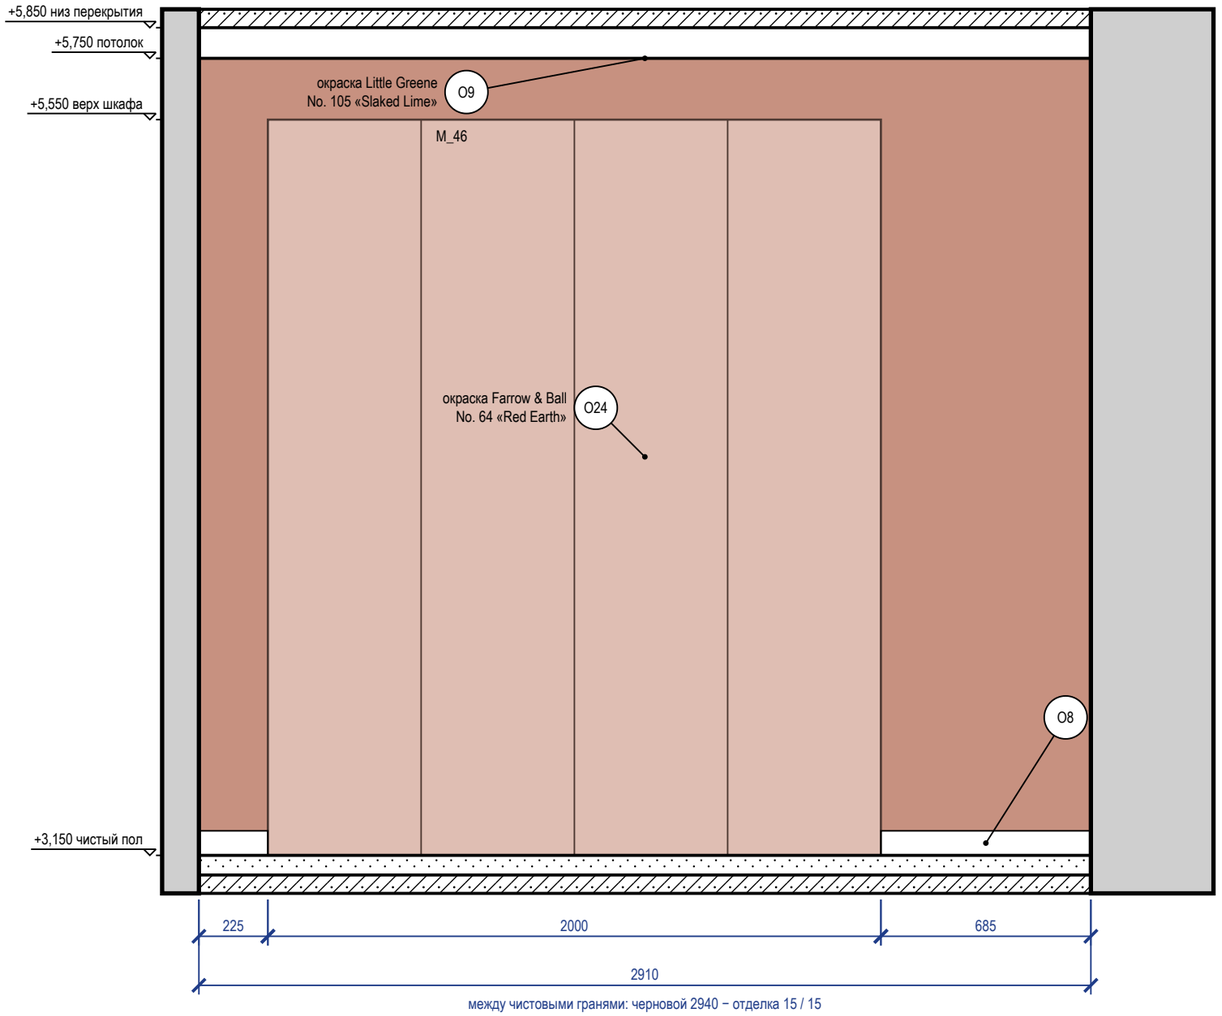


Схема развёрток (М 1:100)

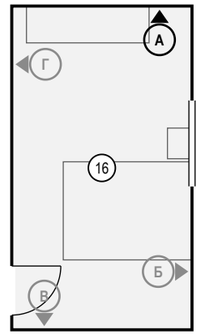


Ведомость отделки (на листе)

Марка	Поверхность	Материал, изделие	Цвет, код	Кол.
O8	плинтус	плинтус МДФ, h 80 мм, аналог: плинтус МДФ под покраску 80×16	Farrow & Ball No. 226 «Joa's White»	0,9 м
O9	потолок	окраска, Little Greene Absolute Matt, глубокоматовая, подготовка Q3	Little Greene No. 105 «Slaked Lime»	15,5 м²
O24	акцентная стена	окраска, Farrow & Ball Modern Emulsion, матовая, подготовка Q3	Farrow & Ball No. 64 «Red Earth»	7,6 м²

4 **Короб стояков К1-1 с люком и звукоизоляцией (М 1:20)**

Узел 4 — лист С9

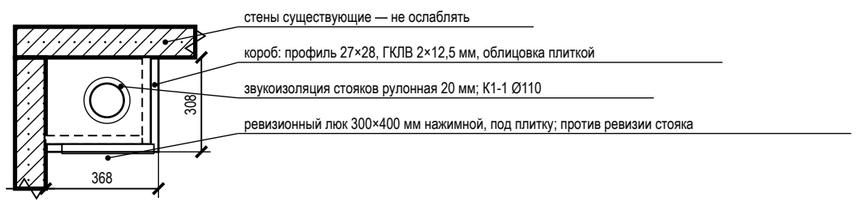


Примечания

1. Размеры — в мм от чистовых поверхностей стен; условные обозначения и общие указания — лист 3.
2. Стена А показана двумя видами: здесь — архитектурная развёртка (мебель, отделка, проёмы, высоты), электроточки и выводы ВК с привязками и таблицей — на листе 127 («Привязки»).
3. Потолок — у каждой стены свой, по плану потолков (ПТ6); ступени — зоной, кромка короба перед нишей — тонкой линией; в поле потолка: ПТ5 +5,650.

					Проект: Дом 331 м²	М 1:20
	Лист	№ док.	Подпись	Дата		
Дизайнер	Кырлан А.С.			04.11.26	Развёртка стены А. Спальня 2 (пом. 16)	


Стадия	Лист	Листов
П	124	168

Развёртка стены Б

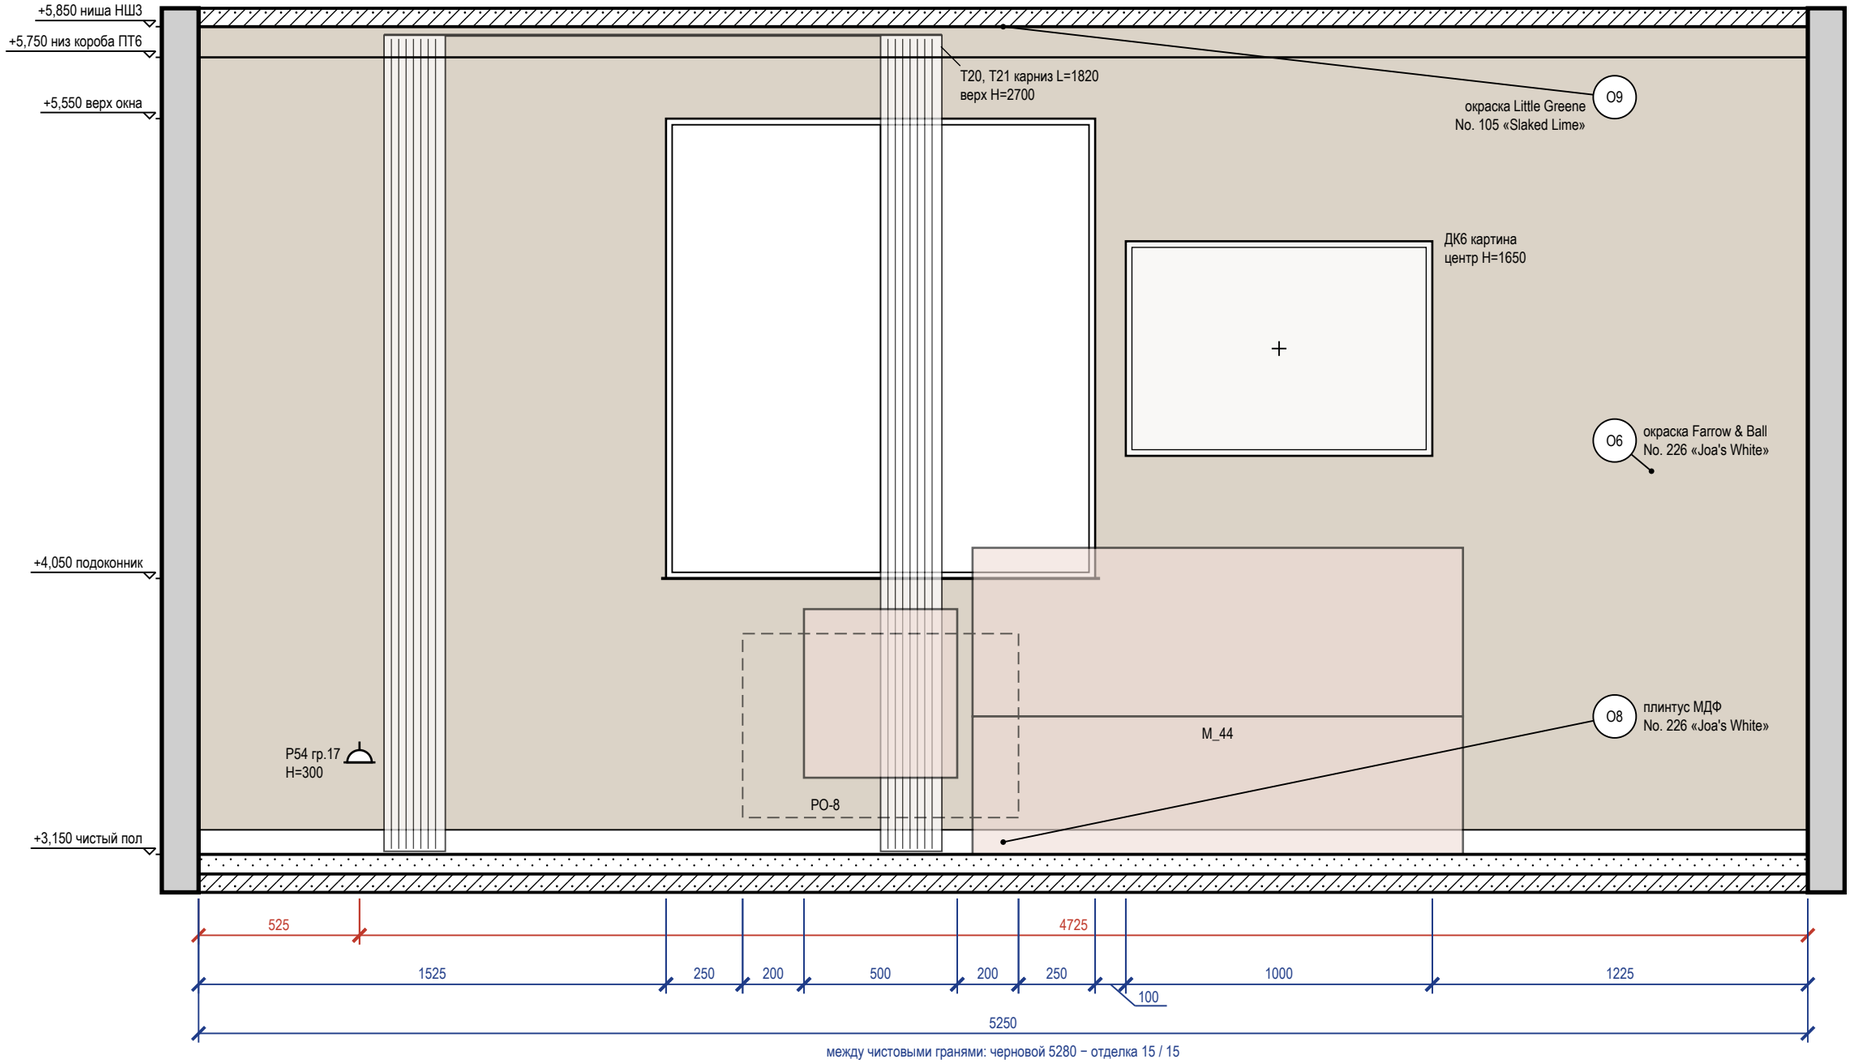

между чистовыми гранями: черновой 5280 − отделка 15 / 15

Схема развёрток (М 1:100)

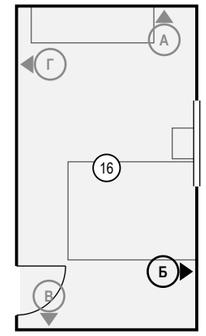

Ведомость отделки (на листе)

Марка	Поверхность	Материал, изделие	Цвет, код	Кол.
О6	стены	окраска, Farrow & Ball Modern Emulsion, матовая, подготовка Q3	Farrow & Ball No. 226 «Joa's White»	12,1 м²
О8	плинтус	плинтус МДФ, h 80 мм, аналог: плинтус МДФ под покраску 80×16	Farrow & Ball No. 226 «Joa's White»	5,3 м
О9	потолок	окраска, Little Greene Absolute Matt, глубокоматовая, подготовка Q3	Little Greene No. 105 «Slaked Lime»	15,5 м²

Примечания

1. Размеры — в мм от чистовых поверхностей стен; условные обозначения и общие указания — лист 3.
2. Картины и зеркала крепить к основанию по паспорту изделия (закладные и анкеры — в перечне скрытых работ); крест — ось центра предмета.
3. Карнизы (шины) — по ведомости текстиля декоратора: длина L и верх H на развёртке — те же числа, что в ведомости; крепление — до окраски потолка.
4. Потолок — у каждой стены свой, по плану потолков (НШ3, ПТ6); ступени — зоной, кромка короба перед нишей — тонкой линией; в поле потолка: ПТ5 +5,650.

	Лист	№ док.	Подпись	Дата
Дизайнер	Кырлан А.С.			04.11.26

Проект: Дом 331 м² — **М 1:20**

Развёртка стены Б. Спальня 2 (пом. 16)

Стадия	Лист	Листов
П	125	168

выпуск 04.11.2026 № f163a372b2 · стр. 125 из 168

Развёртка стены В


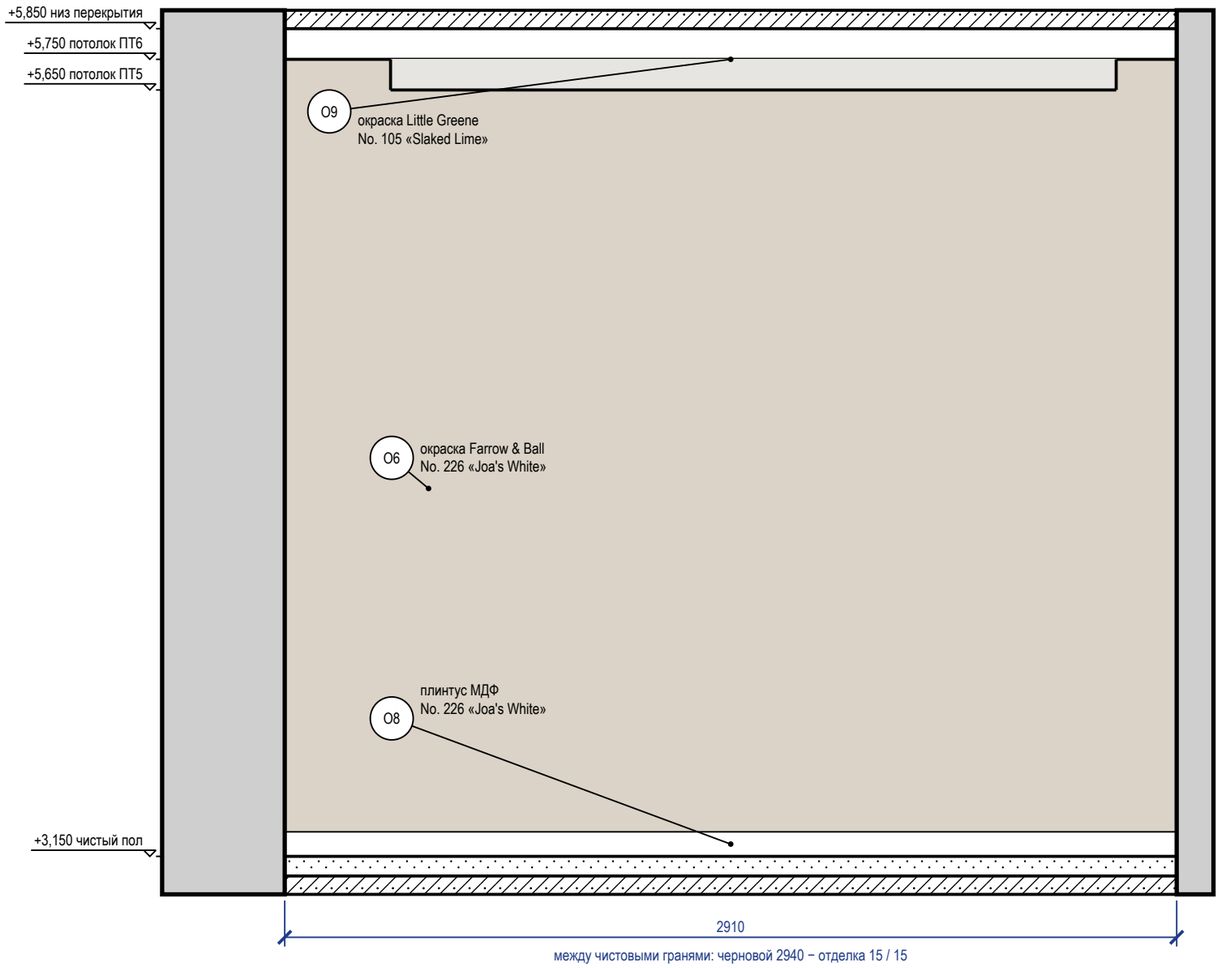


Схема развёрток (М 1:100)

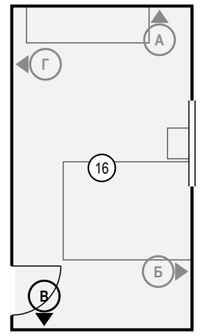

Ведомость отделки (на листе)

Марка	Поверхность	Материал, изделие	Цвет, код	Кол.
О6	стены	окраска, Farrow & Ball Modern Emulsion, матовая, подготовка Q3	Farrow & Ball No. 226 «Joa's White»	7,6 м²
О8	плинтус	плинтус МДФ, h 80 мм, аналог: плинтус МДФ под покраску 80×16	Farrow & Ball No. 226 «Joa's White»	2,9 м
О9	потолок	окраска, Little Greene Absolute Matt, глубокоматовая, подготовка Q3	Little Greene No. 105 «Slaked Lime»	15,5 м²

Примечания

1. Размеры — в мм от чистовых поверхностей стен; условные обозначения и общие указания — лист 3.
2. Стена В показана двумя видами: здесь — архитектурная развёртка (мебель, отделка, проёмы, высоты), электроточки и выводы ВК с привязками и таблицей — на листе 127 («Привязки»).
3. Потолок — у каждой стены свой, по плану потолков (ПТ6, ПТ5); ступени — зоной, кромка короба перед нишей — тонкой линией.


	Лист	№ док.	Подпись	Дата
Дизайнер	Кырлан А.С.			04.11.26

Проект: Дом 331 м² — **М 1:20**

Развёртка стены В. Спальня 2 (пом. 16)

Стадия	Лист	Листов
П	126	168

Развёртка стены А: электроточки и выводы

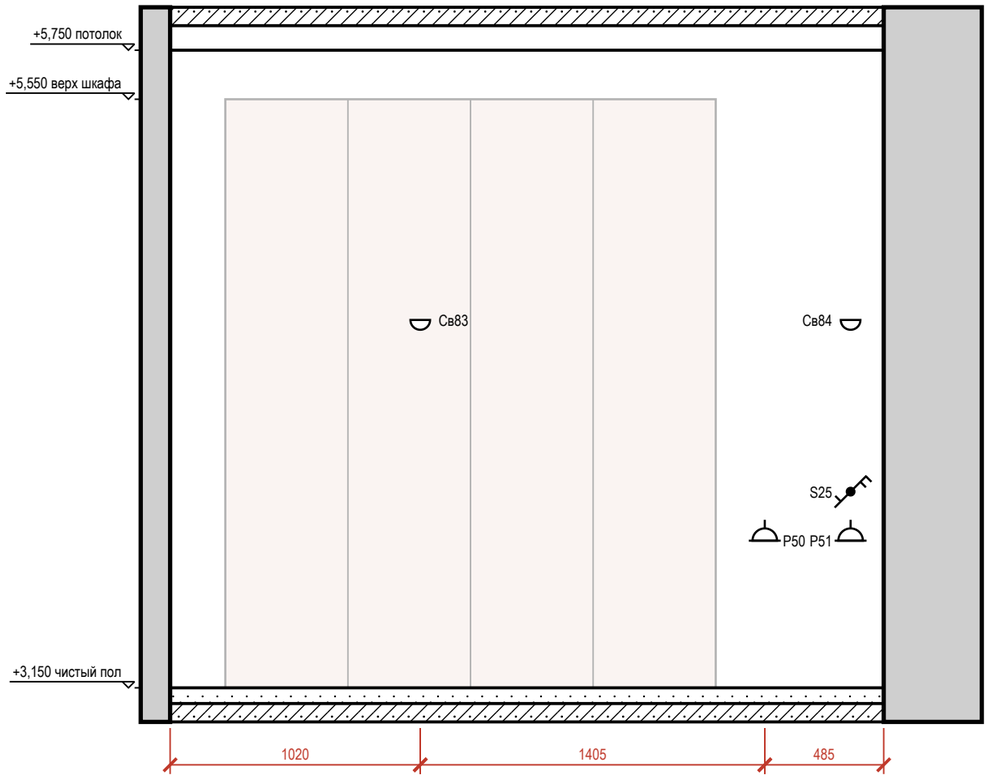

Развёртка стены В: электроточки и выводы

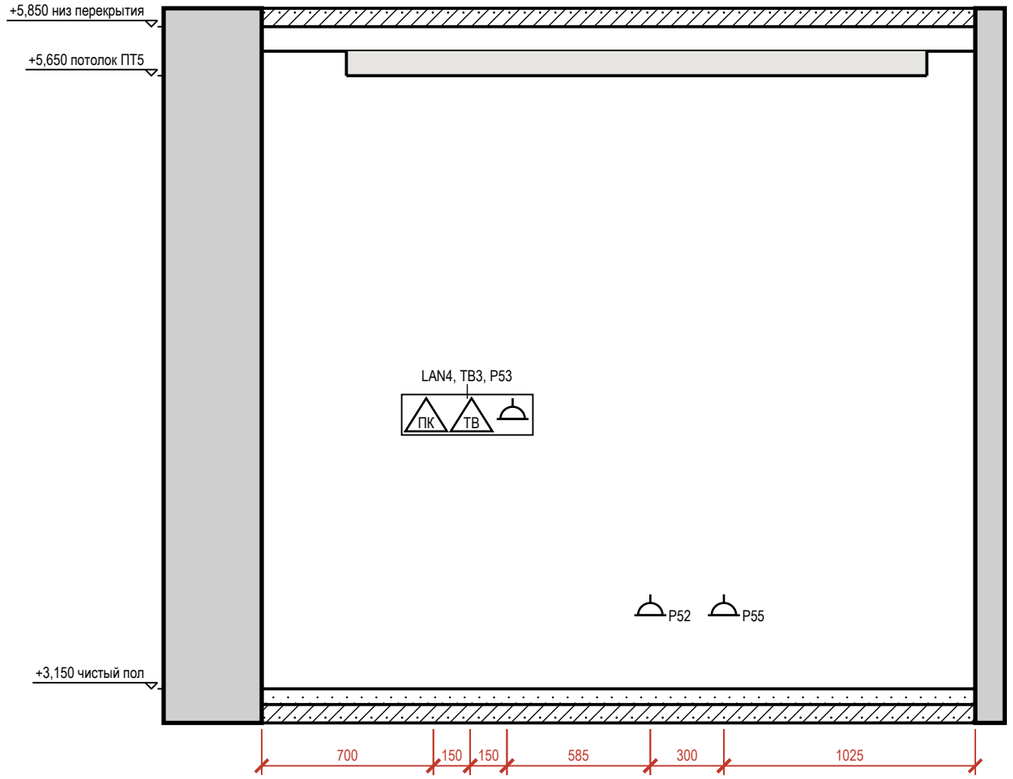



Таблица привязок электроточек и выводов

Стена	Марка	Назначение	От угла, мм	Н от пола, мм	Примечание
A	Св83	светильник настенный	1020	1500	гр. 1
A	P50	розетка: у кровати	2425	600	гр. 17
A	P51	розетка: у кровати	2775	600	гр. 17
A	S25	выключатель	2775	800	гр. 1
A	Св84	светильник настенный	2775	1500	гр. 1
B	LAN4	розетка RJ45: Smart TV	700	1100	
B	TB3	розетка ТВ: ТВ над комодом	850	1100	
B	P53	розетка: ТВ над комодом (в одной зоне с TB3, LAN4)	1000	1100	гр. 17
B	P52	розетка: у комода	1585	300	гр. 17
B	P55	розетка: уборка у входа	1885	300	гр. 17

Условные обозначения

- розетка с заземляющим контактом; у знака — марка, ×N постов в рамке, гр. — группа щита, Н — высота оси, мм
- выключатель одноклавишный
- выключатель двухклавишный (флажков — по числу клавиш)
- выключатель с проходной или перекрёстной клавишей (обратный флажок); тип клавиши — в подписи
- светильник настенный (бра), Н — высота оси
- ПК — розетка компьютерная RJ45
- ТВ — розетка телевизионная
- привязки точек и выводов от угла и от пола, мм
- A — марка развёртки: буква стены, стрелка — взгляд

Схема развёрток (М 1:100)

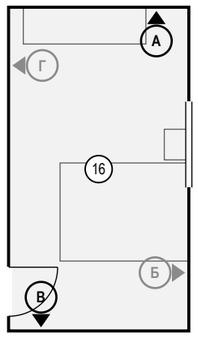

Примечания

1. Вид «Привязки» стен А, В — электроточки и выводы ВК; архитектурная развёртка (мебель, отделка, проёмы, высоты) — на листах 124, 126. Мебель и приборы подложкой для ориентира; их марки и обозначения мебели, проёмов и стен — там же.
2. Привязки — в мм: по горизонтали от левого чистового угла стены до оси изделия, Н — от чистого пола до оси; все точки — в таблице привязок. Красная цепочка — привязки по осям; точки ближе 150 мм одна к другой в цепочку не дробятся — их привязки только в таблице.
3. У знака — марка электроточки (Р — розетка, S — выключатель, Св — светильник, ЭВ — вывод кабеля); условные обозначения и общие указания — лист 3.

					Проект: Дом 331 м² — М 1:25
	Лист	№ док.	Подпись	Дата	Привязки электроточек, стены А, В. Спальня 2 (пом. 16)
Дизайнер	Кырлан А.С.			04.11.26	

Стадия	Лист	Листов
П	127	168

Развёртка стены Г


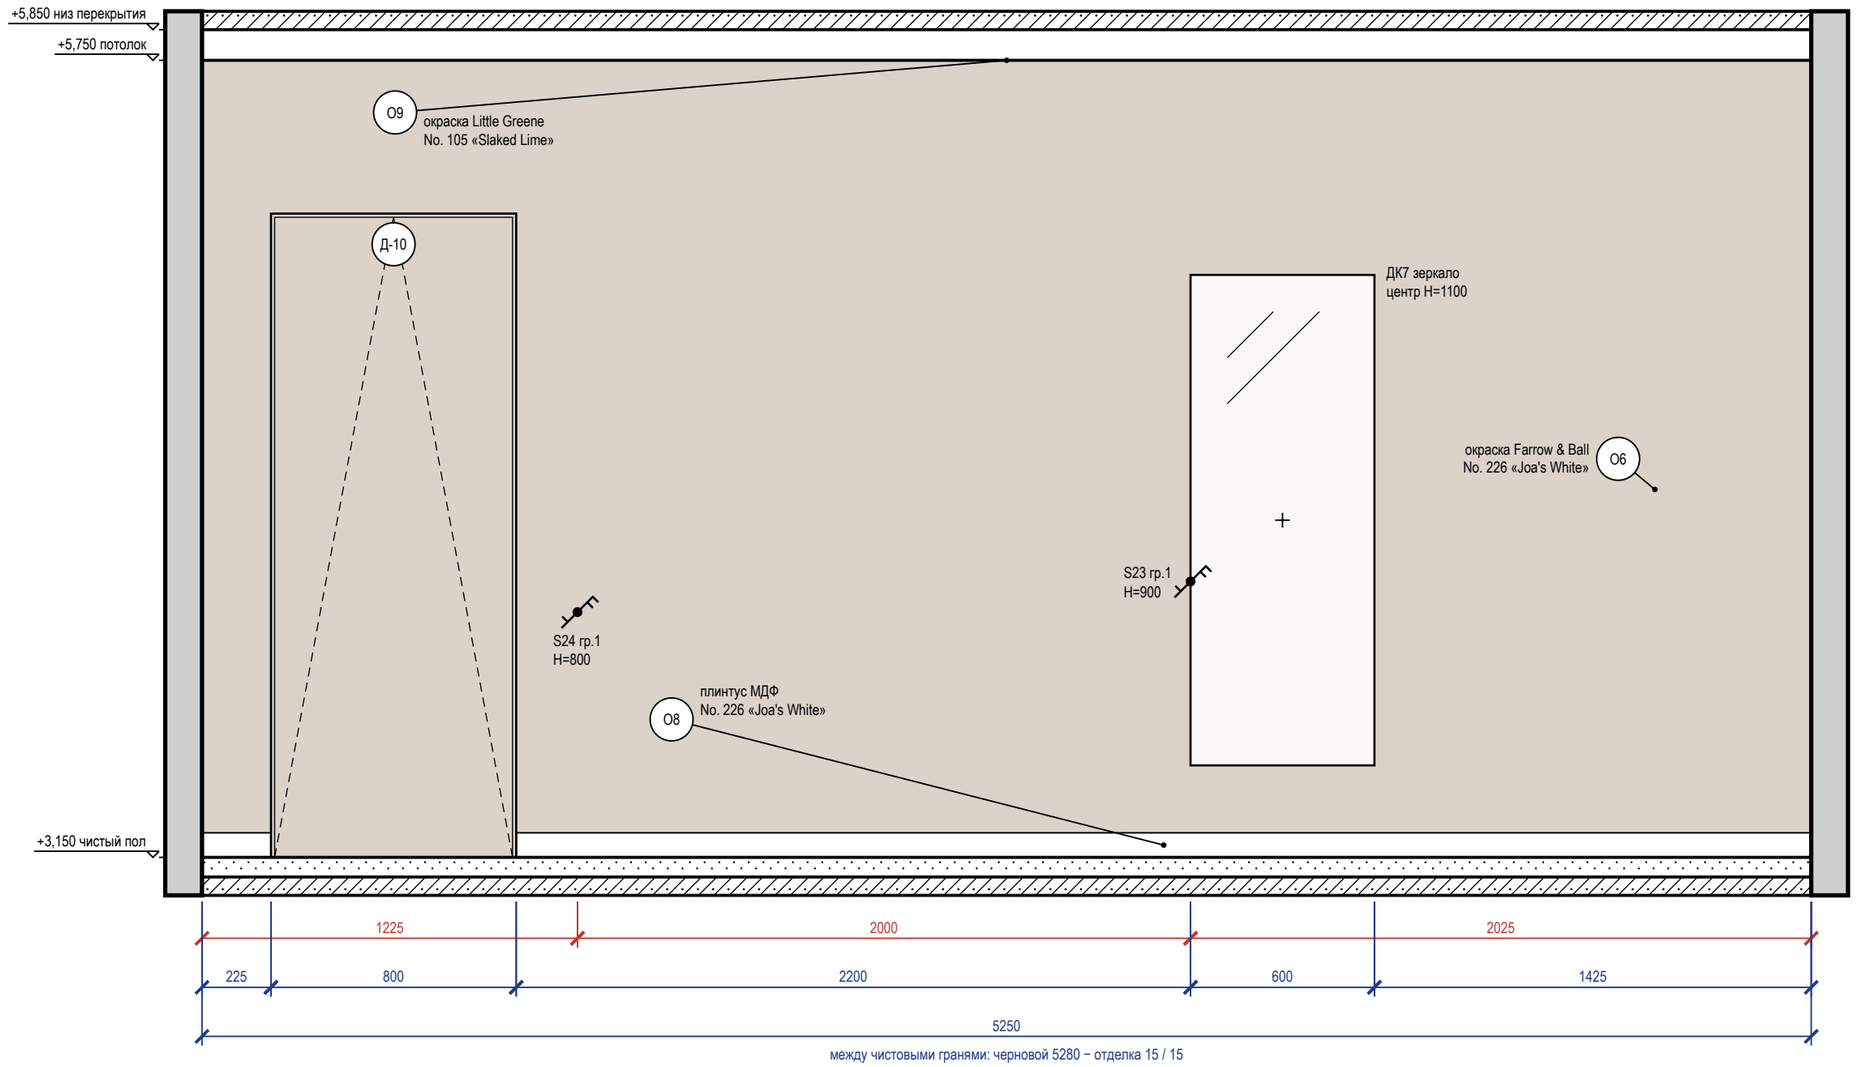


Схема развёрток (М 1:100)

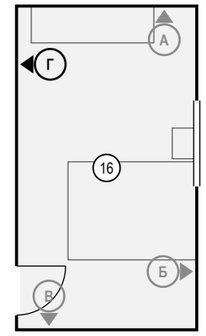

Ведомость отделки (на листе)

Марка	Поверхность	Материал, изделие	Цвет, код	Кол.
О6	стены	окраска, Farrow & Ball Modern Emulsion, матовая, подготовка Q3	Farrow & Ball No. 226 «Joa's White»	12 м²
О8	плинтус	плинтус МДФ, h 80 мм, аналог: плинтус МДФ под покраску 80×16	Farrow & Ball No. 226 «Joa's White»	4,5 м
О9	потолок	окраска, Little Greene Absolute Matt, глубокоматовая, подготовка Q3	Little Greene No. 105 «Slaked Lime»	15,5 м²

Примечания

1. Размеры — в мм от чистовых поверхностей стен; условные обозначения и общие указания — лист 3.
2. Картины и зеркала крепить к основанию по паспорту изделия (закладные и анкеры — в перечне скрытых работ); крест — ось центра предмета.
3. Двери скрытого монтажа — полотно в плоскости стены, отделка стены по полотну, плинтус прерывается у короба (узел — на листе узлов).
4. Потолок — у каждой стены свой, по плану потолков (ПТ6); ступени — зоной, кромка короба перед нишей — тонкой линией; в поле потолка: ПТ5 +5,650.

					Проект: Дом 331 м²	М 1:20
	Лист	№ док.	Подпись	Дата		
Дизайнер	Кырлан А.С.			04.11.26	Развёртка стены Г. Спальня 2 (пом. 16)	Стадия: П; Лист: 128; Листов: 168

выпуск 04.11.2026 № f163a372b2 · стр. 128 из 168

Развёртка стены А


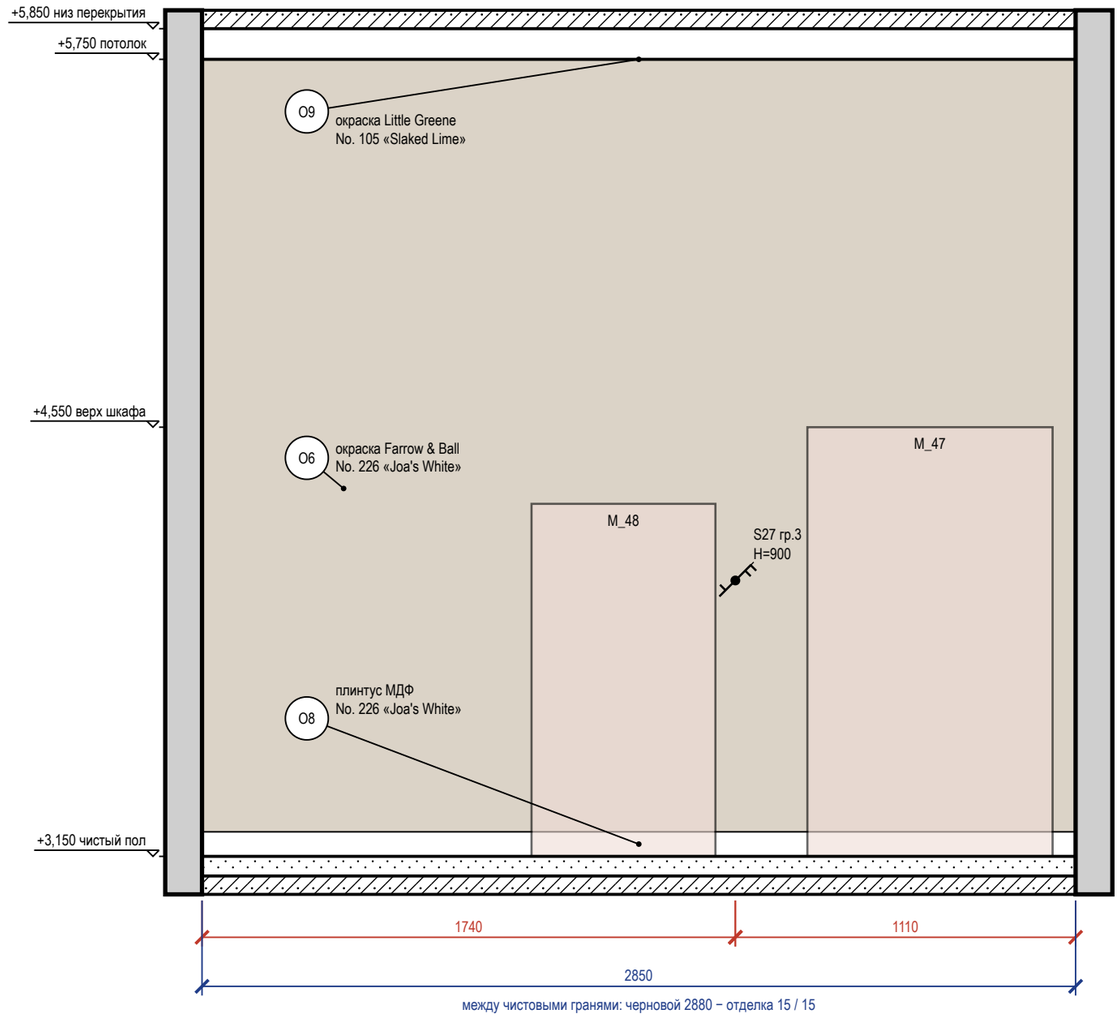


Схема развёрток (М 1:100)

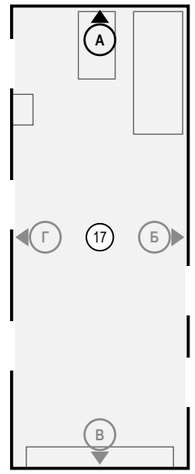

Ведомость отделки (на листе)

Марка	Поверхность	Материал, изделие	Цвет, код	Кол.
О6	стены	окраска, Farrow & Ball Modern Emulsion, матовая, подготовка Q3	Farrow & Ball No. 226 «Joa's White»	7,4 м²
О8	плинтус	плинтус МДФ, h 80 мм, аналог: плинтус МДФ под покраску 80×16	Farrow & Ball No. 226 «Joa's White»	2,9 м
О9	потолок	окраска, Little Greene Absolute Matt, глубокоматовая, подготовка Q3	Little Greene No. 105 «Slaked Lime»	21,7 м²

Примечания

1. Размеры — в мм от чистовых поверхностей стен; условные обозначения и общие указания — лист 3.


	Лист	№ док.	Подпись	Дата
Дизайнер	Кырлан А.С.			04.11.26

Проект: Дом 331 м² — **М 1:20**

Развёртка стены А. Холл мансарды (пом. 17)


Стадия	Лист	Листов
П	129	168

Развёртка стены Б

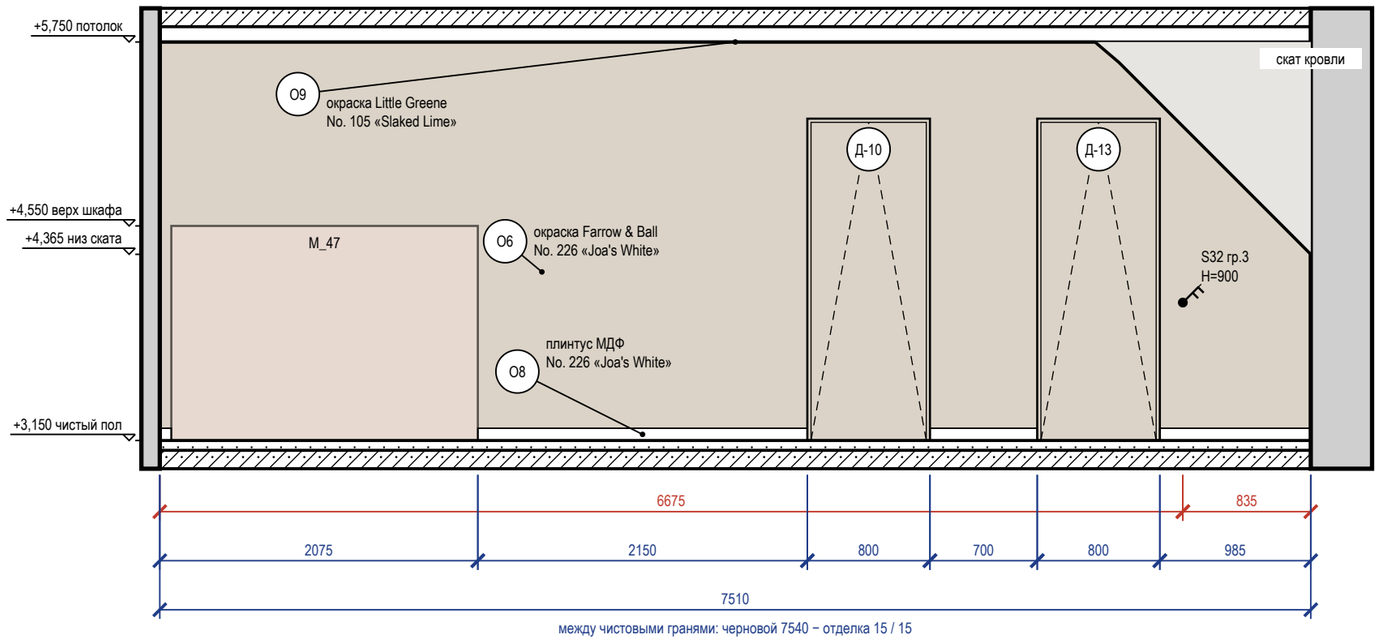

между чистовыми гранями: черновой 7540 − отделка 15 / 15

Схема развёрток (М 1:100)

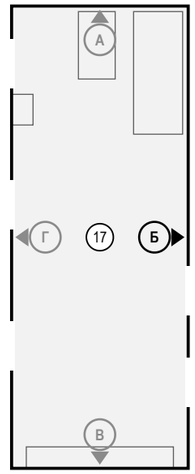

Ведомость отделки (на листе)

Марка	Поверхность	Материал, изделие	Цвет, код	Кол.
О6	стены	окраска, Farrow & Ball Modern Emulsion, матовая, подготовка Q3	Farrow & Ball No. 226 «Joa's White»	16,2 м²
О8	плинтус	плинтус МДФ, h 80 мм, аналог: плинтус МДФ под покраску 80×16	Farrow & Ball No. 226 «Joa's White»	3,9 м
О9	потолок	окраска, Little Greene Absolute Matt, глубокоматовая, подготовка Q3	Little Greene No. 105 «Slaked Lime»	21,7 м²

Примечания

1. Размеры — в мм от чистовых поверхностей стен; условные обозначения и общие указания — лист 3.
2. Двери скрытого монтажа — полотно в плоскости стены, отделка стены по полотну, плинтус прерывается у короба (узел — на листе узлов).

	Лист	№ док.	Подпись	Дата
Дизайнер	Кырлан А.С.			04.11.26

Проект: Дом 331 м² — **М 1:40**

Развёртка стены Б. Холл мансарды (пом. 17)

Стадия	Лист	Листов
П	130	168

Развёртка стены В


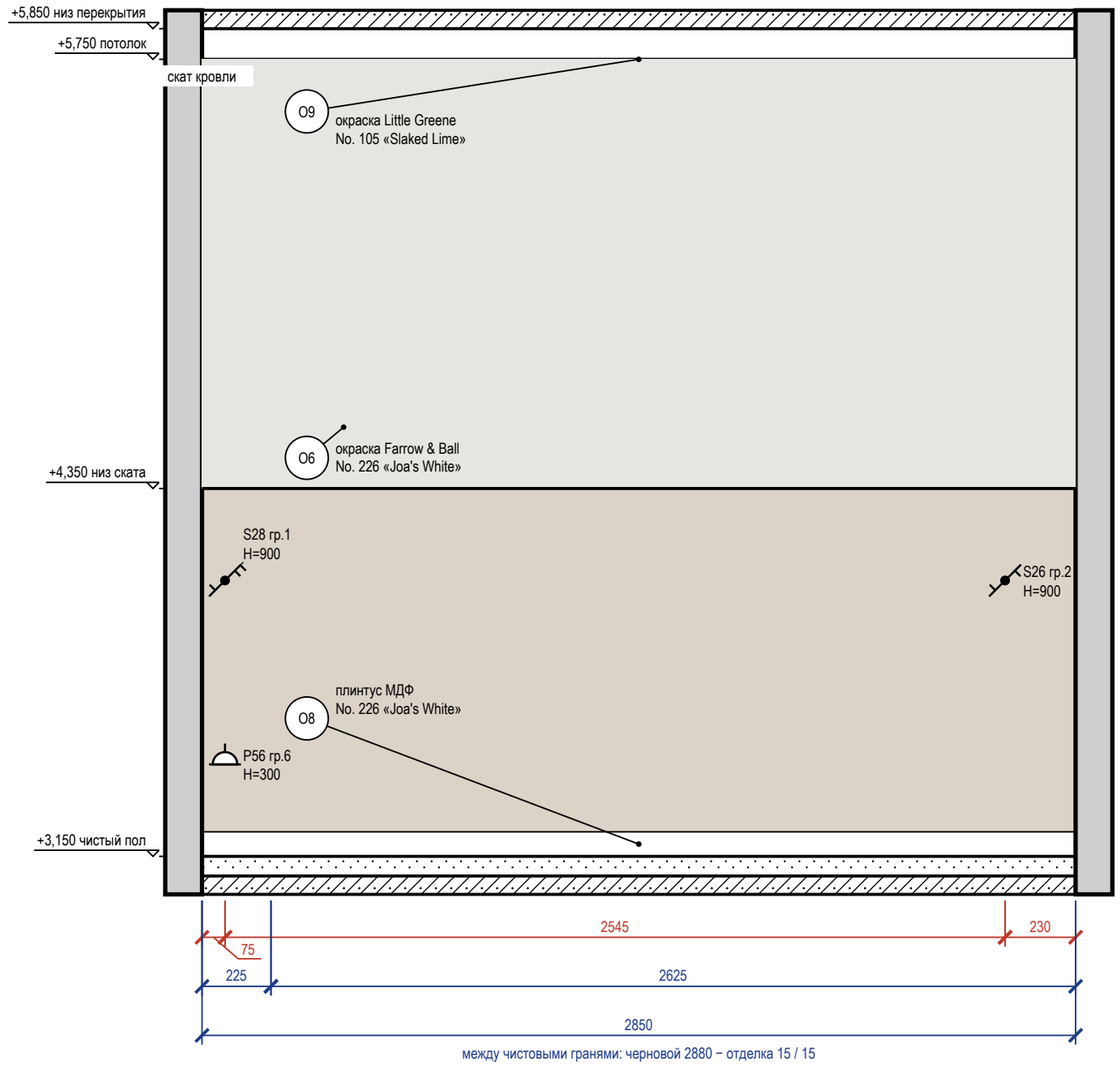


Схема развёрток (М 1:100)

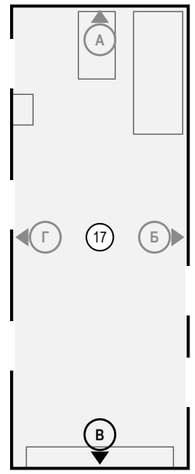

Ведомость отделки (на листе)

Марка	Поверхность	Материал, изделие	Цвет, код	Кол.
О6	стены	окраска, Farrow & Ball Modern Emulsion, матовая, подготовка Q3	Farrow & Ball No. 226 «Joa's White»	7,4 м²
О8	плинтус	плинтус МДФ, h 80 мм, аналог: плинтус МДФ под покраску 80×16	Farrow & Ball No. 226 «Joa's White»	2,9 м
О9	потолок	окраска, Little Greene Absolute Matt, глубокоматовая, подготовка Q3	Little Greene No. 105 «Slaked Lime»	21,7 м²


Примечания

1. Размеры — в мм от чистовых поверхностей стен; условные обозначения и общие указания — лист 3.
2. Схема мебели, приборов и декора не является технической документацией для производства мебели; габариты — по паспортам изделий.

					Проект: Дом 331 м² — М 1:20
	Лист	№ док.	Подпись	Дата	Развёртка стены В. Холл мансарды (пом. 17)
Дизайнер	Кырлан А.С.			04.11.26	


Стадия	Лист	Листов
П	131	168

Развёртка стены Г

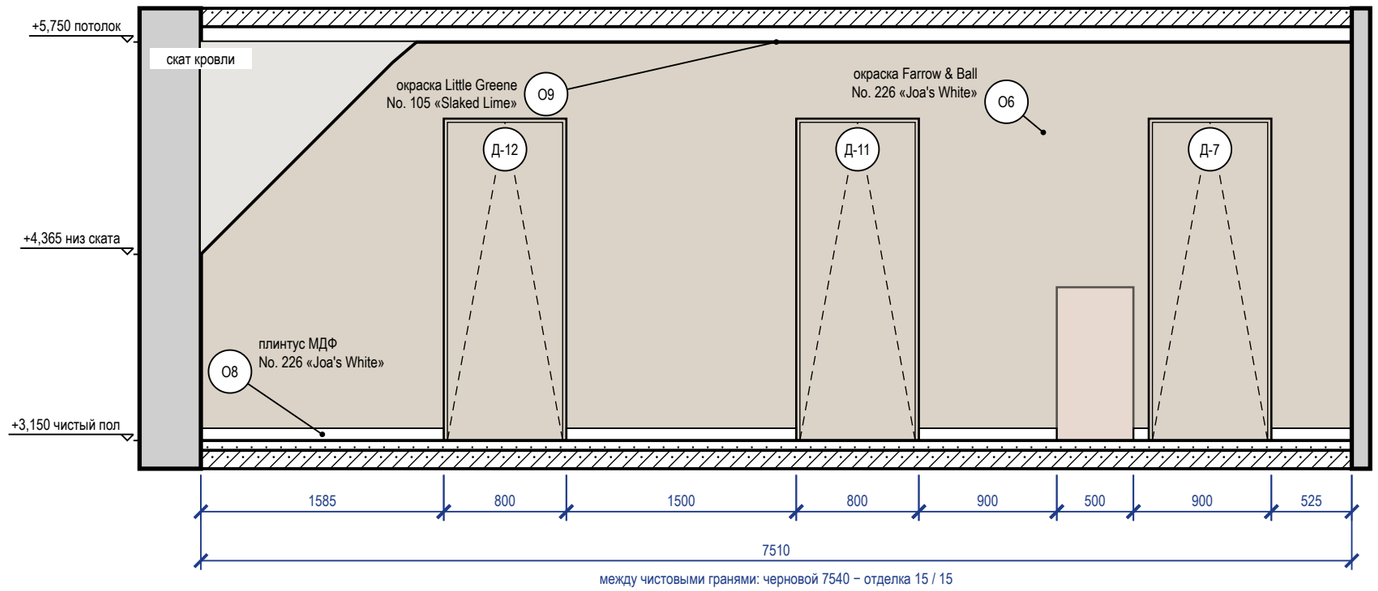

между чистовыми гранями: черновой 7540 − отделка 15 / 15

Схема развёрток (М 1:100)

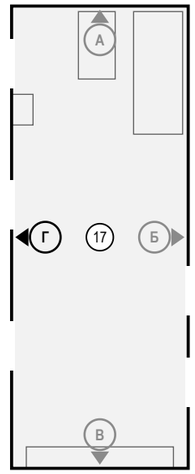

Ведомость отделки (на листе)

Марка	Поверхность	Материал, изделие	Цвет, код	Кол.
О6	стены	окраска, Farrow & Ball Modern Emulsion, матовая, подготовка Q3	Farrow & Ball No. 226 «Joa's White»	14,5 м²
О8	плинтус	плинтус МДФ, h 80 мм, аналог: плинтус МДФ под покраску 80×16	Farrow & Ball No. 226 «Joa's White»	4,6 м
О9	потолок	окраска, Little Greene Absolute Matt, глубокоматовая, подготовка Q3	Little Greene No. 105 «Slaked Lime»	21,7 м²

Примечания

1. Размеры — в мм от чистовых поверхностей стен; условные обозначения и общие указания — лист 3.
2. Двери скрытого монтажа — полотно в плоскости стены, отделка стены по полотну, плинтус прерывается у короба (узел — на листе узлов).

	Лист	№ док.	Подпись	Дата
Дизайнер	Кырлан А.С.			04.11.26

Проект: Дом 331 м² — **М 1:40**

Развёртка стены Г. Холл мансарды (пом. 17)

Стадия	Лист	Листов
П	132	168

Развёртка стены А


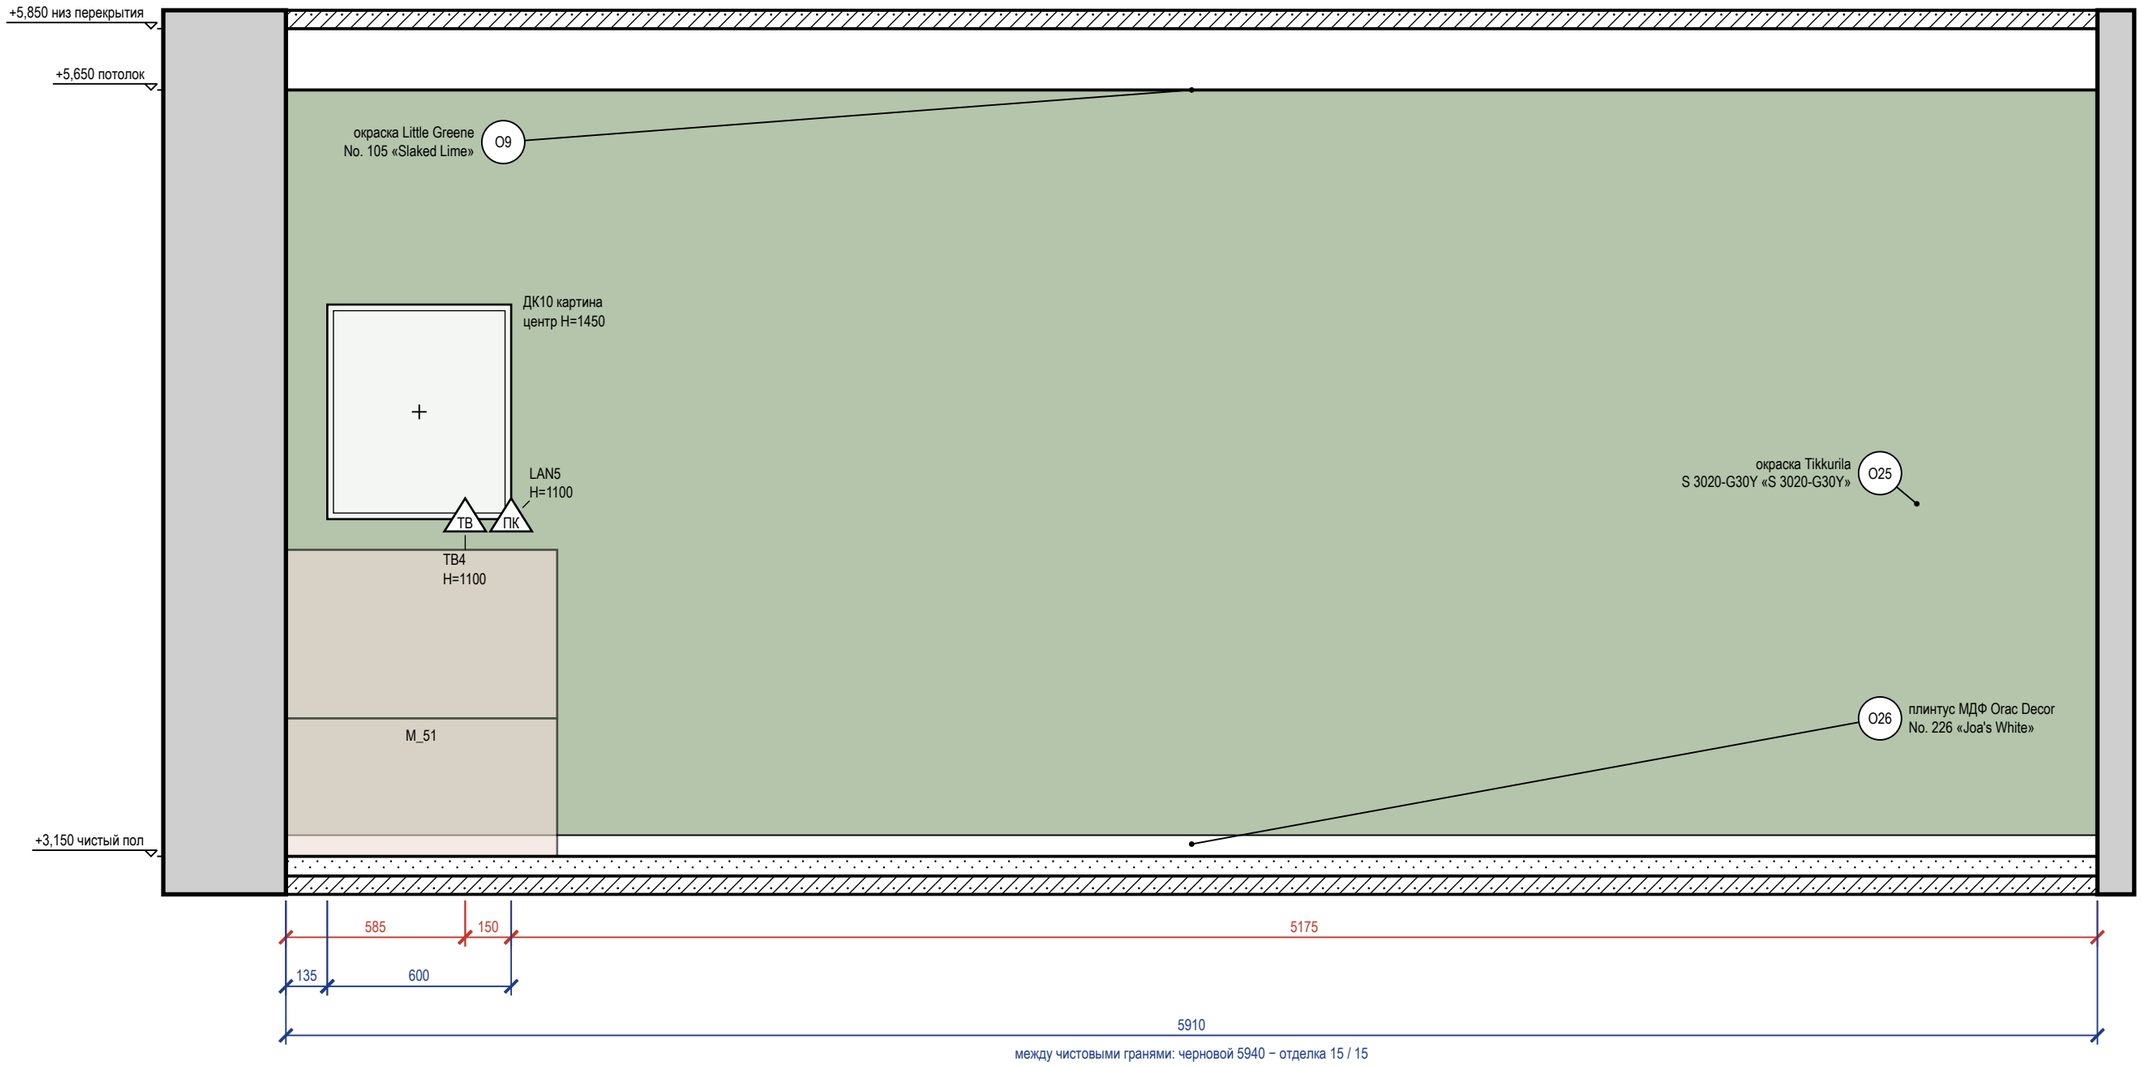


Схема развёрток (М 1:100)

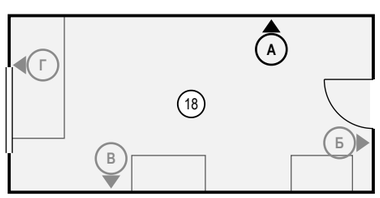

Ведомость отделки (на листе)


Марка	Поверхность	Материал, изделие	Цвет, код	Кол.
O9	потолок	окраска, Little Greene Absolute Matt, глубокоматовая, подготовка Q3	Little Greene No. 105 «Slaked Lime»	17,1 м²
O25	акцентная стена	окраска, Tikkurila Optiva 5 Matt, матовая, подготовка Q3	NCS S 3020-G30Y «S 3020-G30Y»	14,8 м²
O26	плинтус	плинтус МДФ, Orac Decor Contour (Luxxus), h 69 мм, SX165	Farrow & Ball No. 226 «Joa's White»	5,9 м

Примечания

1. Размеры — в мм от чистовых поверхностей стен; условные обозначения и общие указания — лист 3.
2. Картины и зеркала крепить к основанию по паспорту изделия (закладные и анкеры — в перечне скрытых работ); крест — ось центра предмета.
3. Потолок — у каждой стены свой, по плану потолков (ПТ5); ступени — зоной, кромка короба перед нишей — тонкой линией; в поле потолка: ПТ6 +5,750.


					Проект: Дом 331 м² — М 1:20
	Лист	№ док.	Подпись	Дата	Развёртка стены А. Спальня 3 (пом. 18)
Дизайнер	Кырлан А.С.			04.11.26	Стадия: П; Лист: 133; Листов: 168

Развёртка стены Б

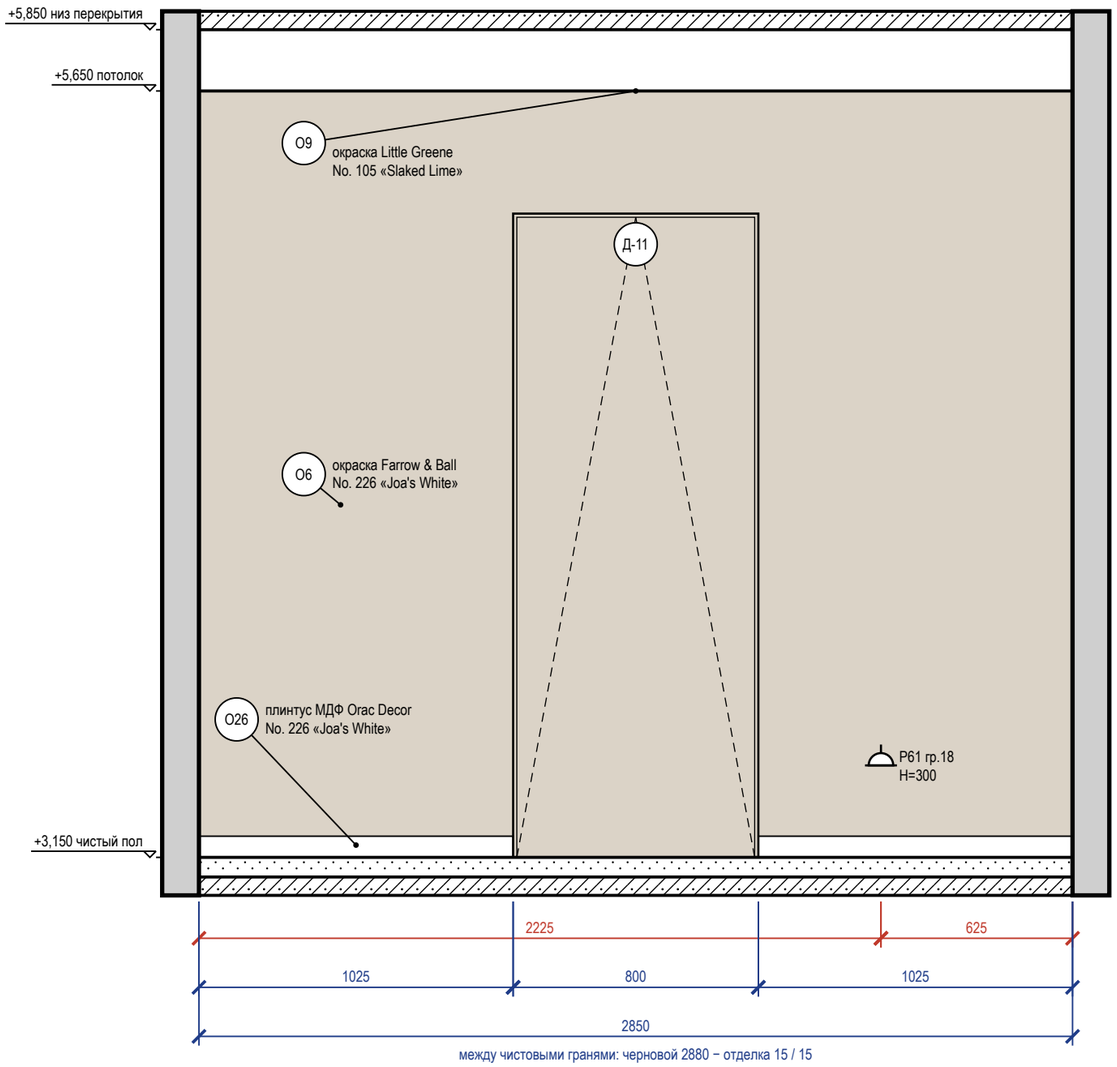


между чистовыми гранями: черновой 2880 − отделка 15 / 15

Развёртка стены Г

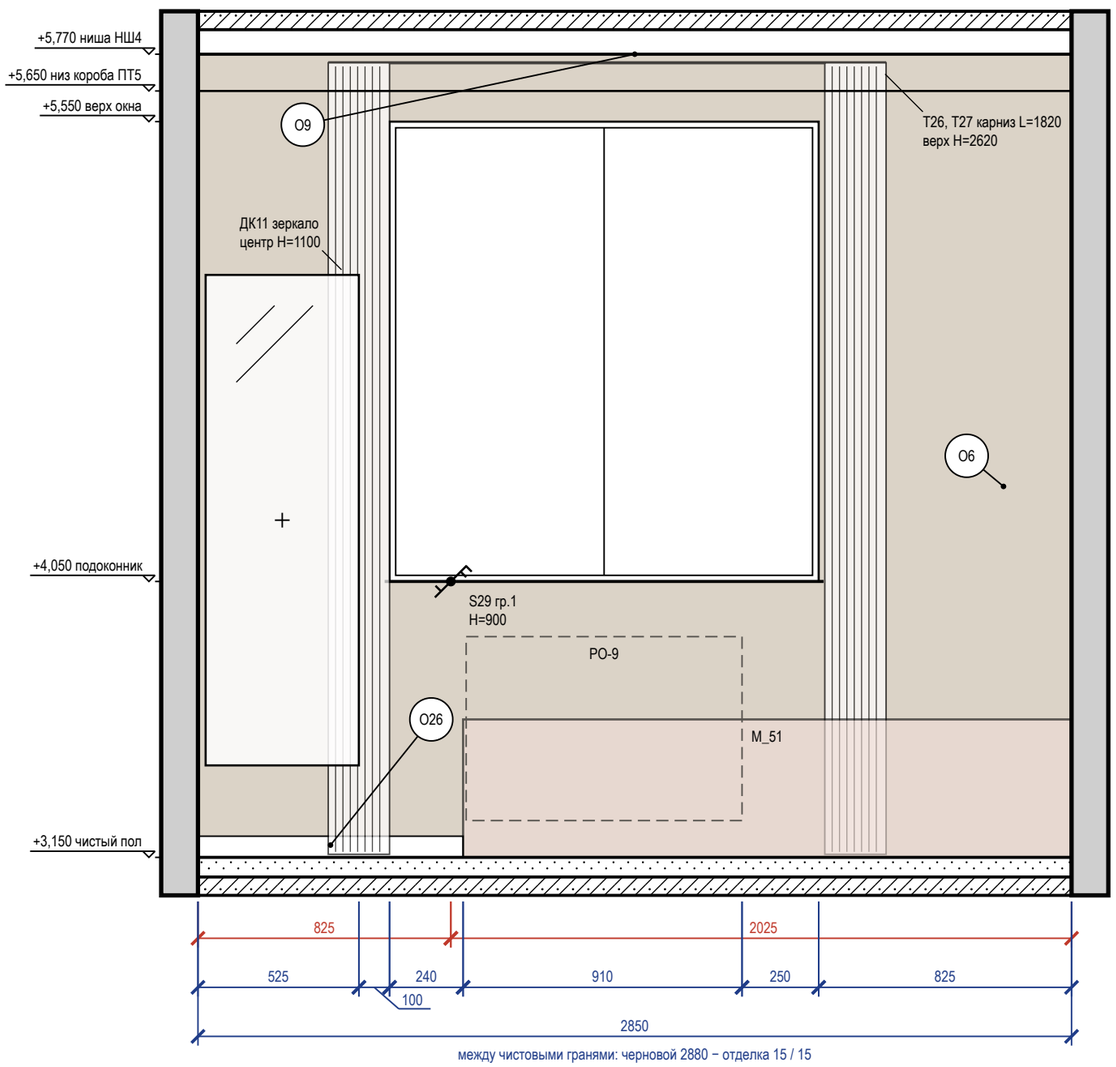

между чистовыми гранями: черновой 2880 − отделка 15 / 15

Схема развёрток (М 1:100)

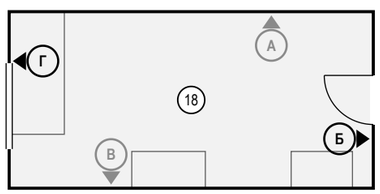

Ведомость отделки (на листе)

Марка	Поверхность	Материал, изделие	Цвет, код	Кол.
О6	стены	окраска, Farrow & Ball Modern Emulsion, матовая, подготовка Q3	Farrow & Ball No. 226 «Joa's White»	10,8 м²
О9	потолок	окраска, Little Greene Absolute Matt, глубокоматовая, подготовка Q3	Little Greene No. 105 «Slaked Lime»	17,1 м²
О26	плинтус	плинтус МДФ, Orac Decor Contour (Luxxus), h 69 мм, SX165	Farrow & Ball No. 226 «Joa's White»	2,9 м

Примечания

1. Размеры — в мм от чистовых поверхностей стен; условные обозначения и общие указания — лист 3.
2. Картины и зеркала крепить к основанию по паспорту изделия (закладные и анкеры — в перечне скрытых работ); крест — ось центра предмета.
3. Карнизы (шины) — по ведомости текстиля декоратора: длина L и верх Н на развёртке — те же числа, что в ведомости; крепление — до окраски потолка.
4. Двери скрытого монтажа — полотно в плоскости стены, отделка стены по полотну, плинтус прерывается у короба (узел — на листе узлов).
5. Потолок — у каждой стены свой, по плану потолков (ПТ5, НШ4); ступени — зоной, кромка короба перед нишей — тонкой линией; в поле потолка: ПТ6 +5,750.


	Лист	№ док.	Подпись	Дата
Дизайнер	Кырлан А.С.			04.11.26

Проект: Дом 331 м² — **М 1:20**

Развёртки стен Б, Г. Спальня 3 (пом. 18)


Стадия	Лист	Листов
П	134	168

Развёртка стены В

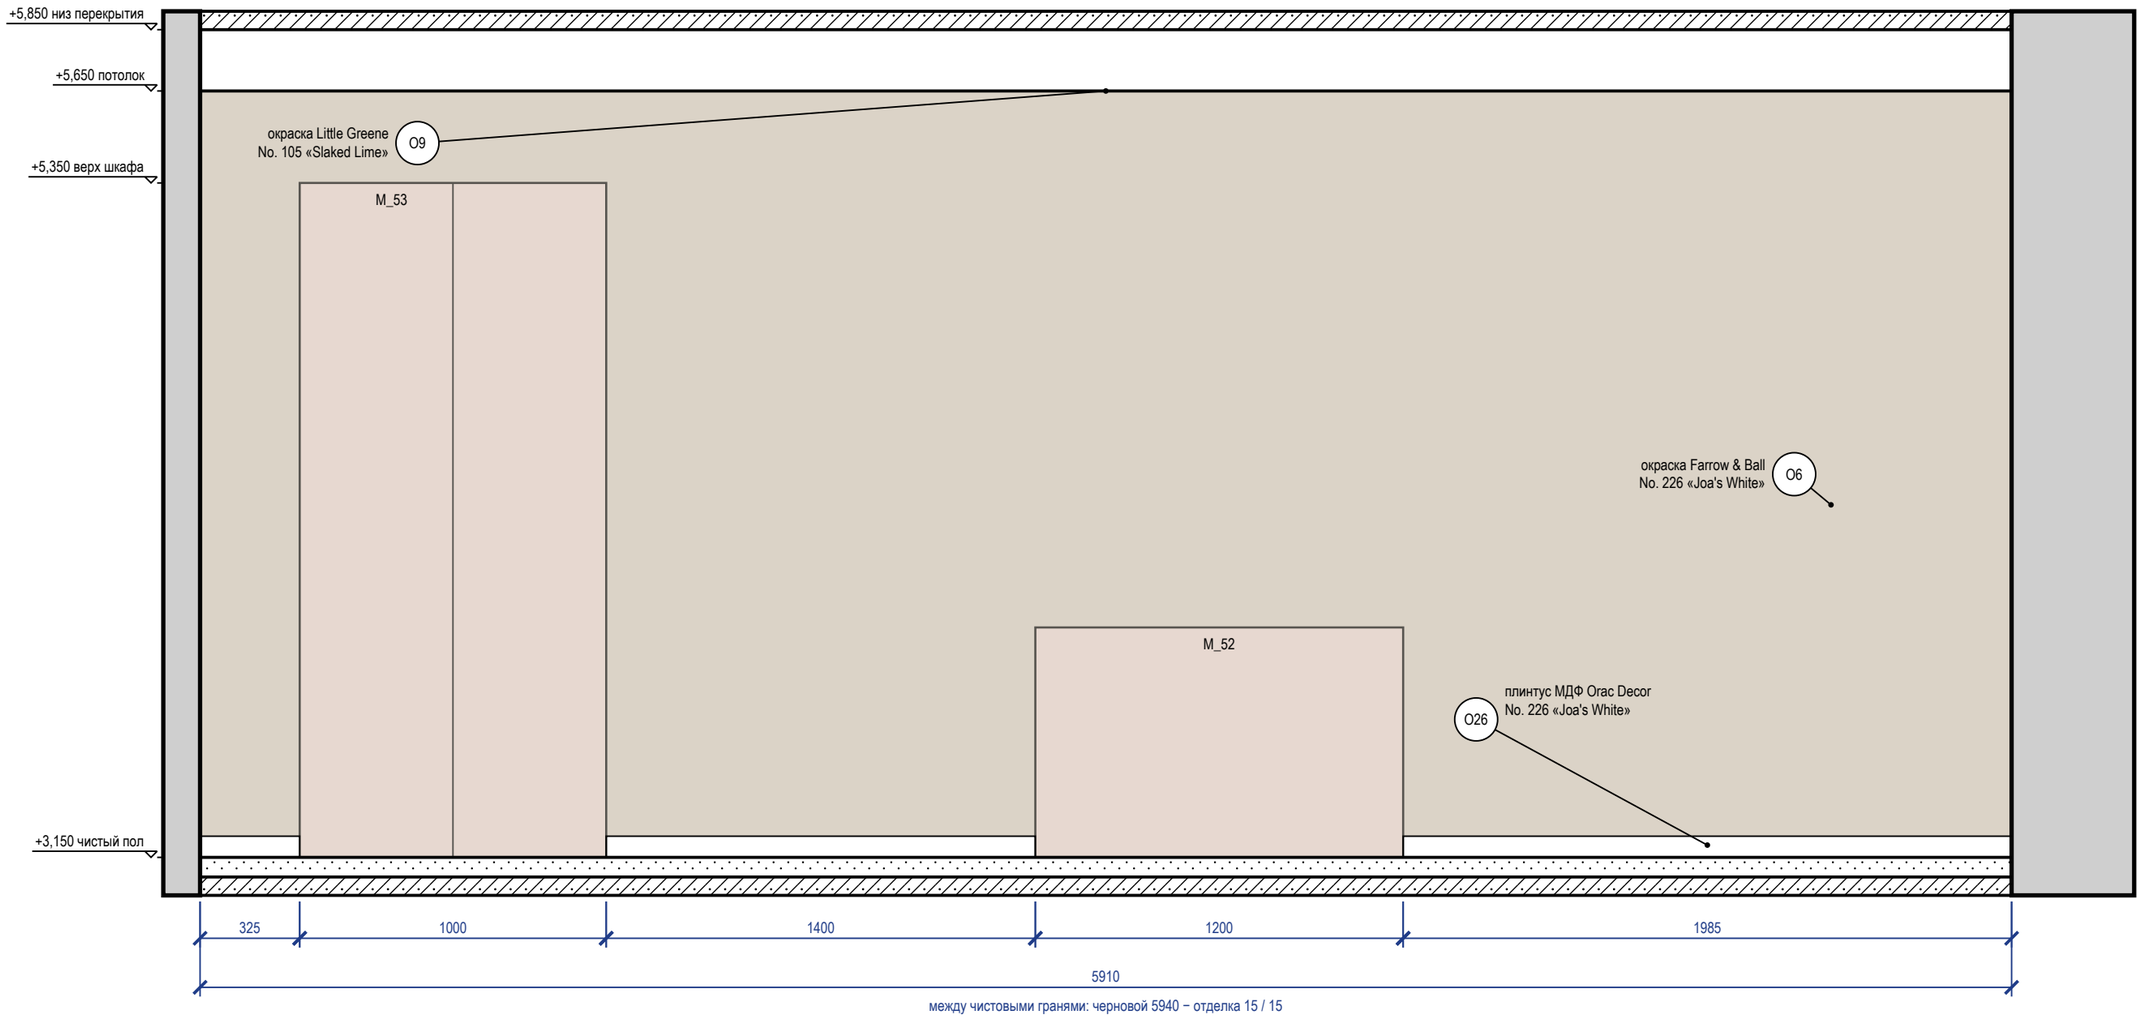

между чистовыми гранями: черновой 5940 − отделка 15 / 15

Схема развёрток (М 1:100)

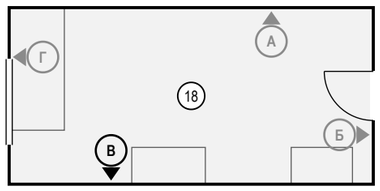

Ведомость отделки (на листе)

Марка	Поверхность	Материал, изделие	Цвет, код	Кол.
O6	стены	окраска, Farrow & Ball Modern Emulsion, матовая, подготовка Q3	Farrow & Ball No. 226 «Joa's White»	14,8 м²
O9	потолок	окраска, Little Greene Absolute Matt, глубокоматовая, подготовка Q3	Little Greene No. 105 «Slaked Lime»	17,1 м²
O26	плинтус	плинтус МДФ, Orac Decor Contour (Luxxus), h 69 мм, SX165	Farrow & Ball No. 226 «Joa's White»	3,7 м

Примечания

1. Размеры — в мм от чистовых поверхностей стен; условные обозначения и общие указания — лист 3.
2. Стена В показана двумя видами: здесь — архитектурная развёртка (мебель, отделка, проёмы, высоты), электроточки и выводы ВК с привязками и таблицей — на листе 136 («Привязки»).
3. Потолок — у каждой стены свой, по плану потолков (ПТ5); ступени — зоной, кромка короба перед нишей — тонкой линией; в поле потолка: ПТ6 +5,750.

					Проект: Дом 331 м²	М 1:20
	Лист	№ док.	Подпись	Дата		
Дизайнер	Кырлан А.С.			04.11.26	Развёртка стены В. Спальня 3 (пом. 18)	

Стадия	Лист	Листов
П	135	168

Развёртка стены В: электроточки и выводы

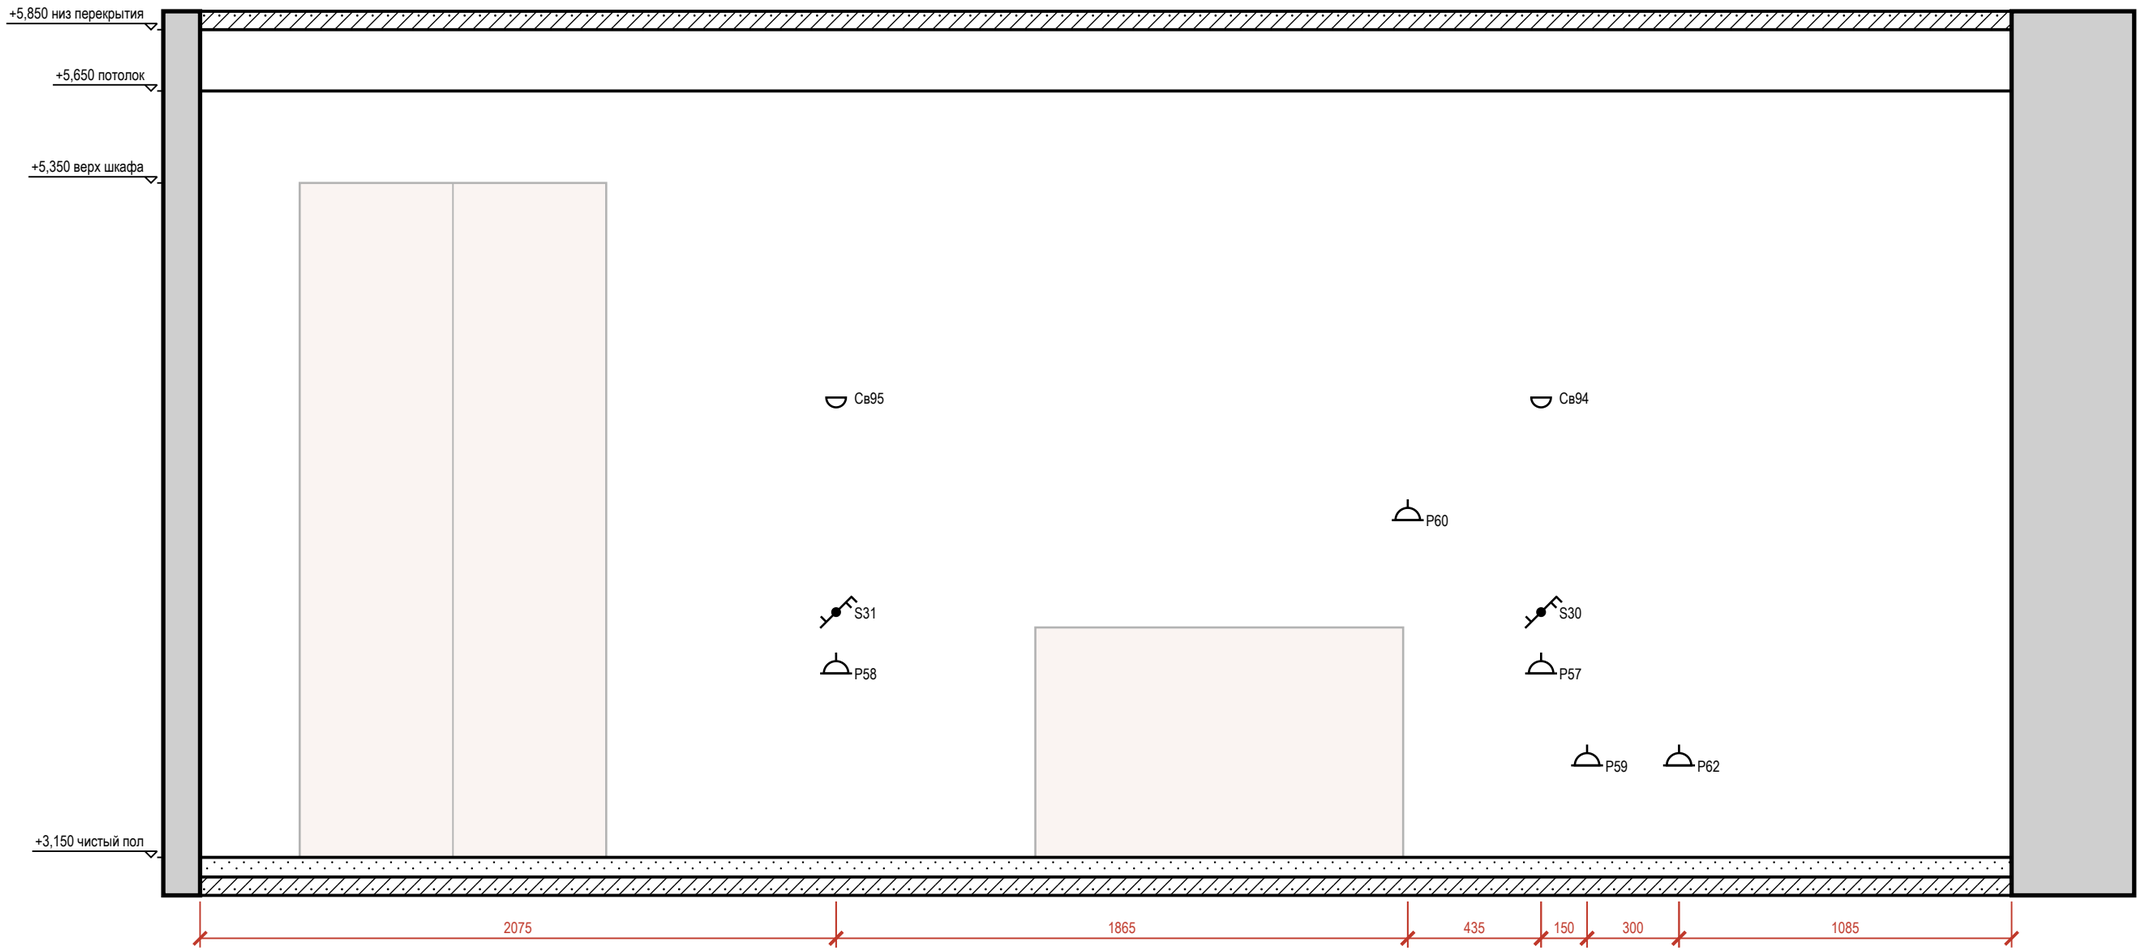



Таблица привязок электроточек и выводов

Марка	Назначение	От угла, мм	Н от пола, мм	Примечание
P58	розетка: у кровати	2075	600	гр. 18
S31	выключатель	2075	800	гр. 1
Св95	светильник настенный	2075	1500	гр. 1
P60	розетка: ТВ над комодом (в одной зоне с ТВ4, LAN5)	3940	1100	гр. 18
P57	розетка: у кровати	4375	600	гр. 18
S30	выключатель	4375	800	гр. 1
Св94	светильник настенный	4375	1500	гр. 1
P59	розетка: у комода	4525	300	гр. 18
P62	розетка: уборка у входа	4825	300	гр. 18

Условные обозначения

- розетка с заземляющим контактом; у знака — марка, ×N постов в рамке, гр. — группа щита, Н — высота оси, мм
- выключатель одноклавишный
- выключатель двухклавишный (флажков — по числу клавиш)
- выключатель с проходной или перекрёстной клавишей (обратный флажок); тип клавиши — в подписи
- светильник настенный (бра), Н — высота оси
- привязки точек и выводов от угла и от пола, мм
- А — марка развёртки: буква стены, стрелка — взгляд

Схема развёрток (М 1:100)

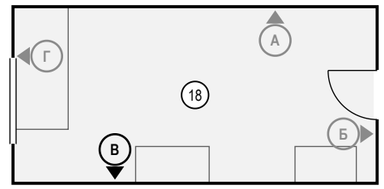

Примечания

1. Вид «Привязки» стены В — электроточки и выводы ВК; архитектурная развёртка (мебель, отделка, проёмы, высоты) — на листе 135. Мебель и приборы — подложкой для ориентира; их марки и обозначения мебели, проёмов и стен — там же.
2. Привязки — в мм: по горизонтали от левого чистового угла стены до оси изделия, Н — от чистого пола до оси; все точки — в таблице привязок. Красная цепочка — привязки по осям; точки ближе 120 мм одна к другой в цепочку не дробятся — их привязки только в таблице.
3. У знака — марка электроточки (Р — розетка, S — выключатель, Св — светильник, ЭВ — вывод кабеля); условные обозначения и общие указания — лист 3.

					Проект: Дом 331 м²	М 1:20
	Лист	№ док.	Подпись	Дата	Привязки электроточек, стена В. Спальня 3 (пом. 18)	Стадия: П; Лист: 136; Листов: 168
Дизайнер	Кырлан А.С.			04.11.26		

Развёртка стены А


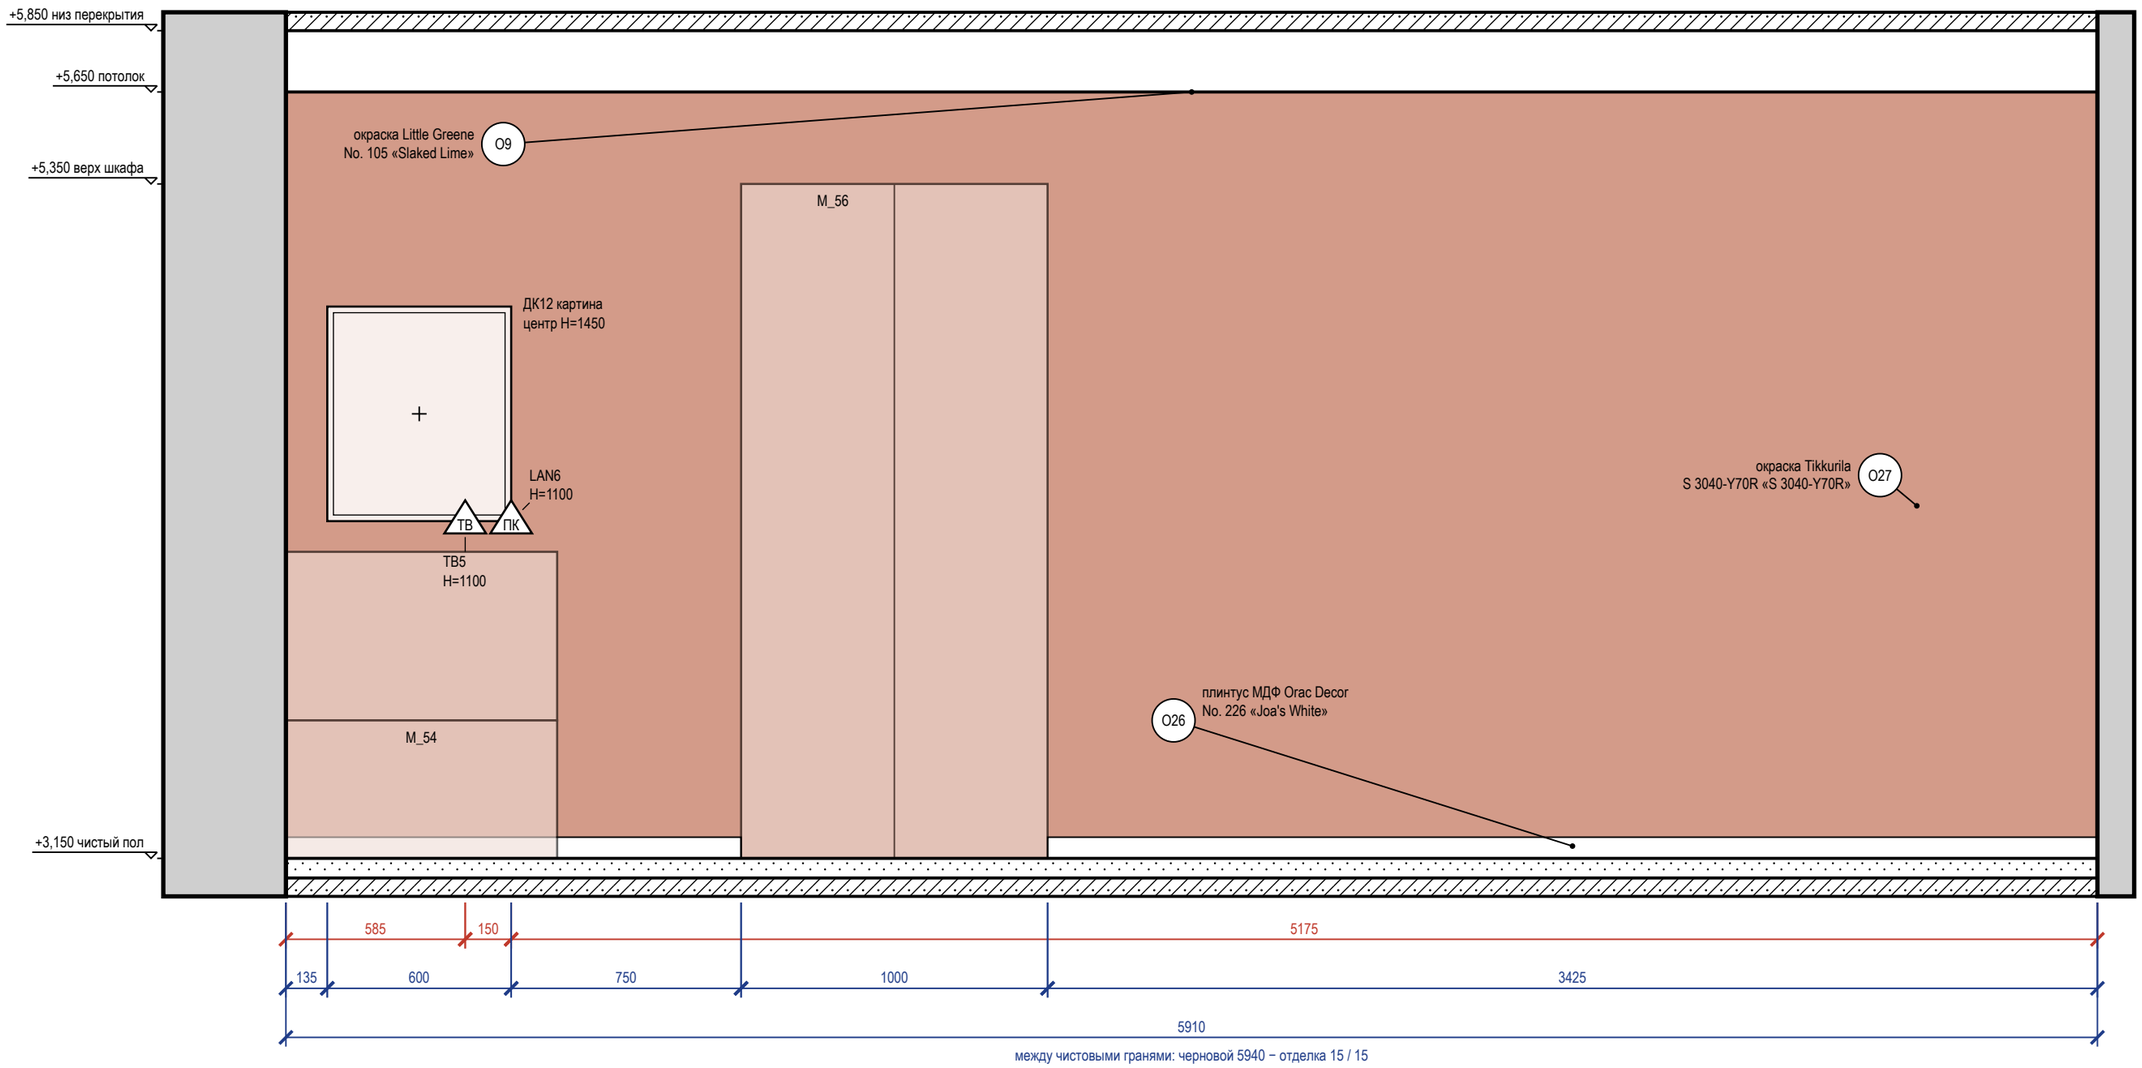


Схема развёрток (М 1:100)

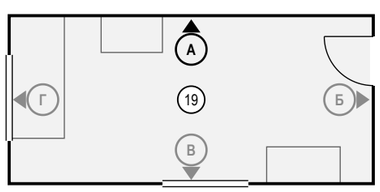

Ведомость отделки (на листе)

Марка	Поверхность	Материал, изделие	Цвет, код	Кол.
O9	потолок	окраска, Little Greene Absolute Matt, глубокоматовая, подготовка Q3	Little Greene No. 105 «Slaked Lime»	16,3 м²
O26	плинтус	плинтус МДФ, Orac Decor Contour (Luxxus), h 69 мм, SX165	Farrow & Ball No. 226 «Joa's White»	4,9 м
O27	акцентная стена	окраска, Tikkurila Optiva 5 Matt, матовая, подготовка Q3	NCS S 3040-Y70R «S 3040-Y70R»	14,8 м²

Примечания

1. Размеры — в мм от чистовых поверхностей стен; условные обозначения и общие указания — лист 3.
2. Картины и зеркала крепить к основанию по паспорту изделия (закладные и анкеры — в перечне скрытых работ); крест — ось центра предмета.
3. Потолок — у каждой стены свой, по плану потолков (ПТ5); ступени — зоной, кромка короба перед нишей — тонкой линией; в поле потолка: ПТ6 +5,750.

	Лист	№ док.	Подпись	Дата
Дизайнер	Кырлан А.С.			04.11.26

Проект: Дом 331 м² — **М 1:20**

Развёртка стены А. Спальня 4 (пом. 19)

Стадия	Лист	Листов
П	137	168

Развёртка стены Б


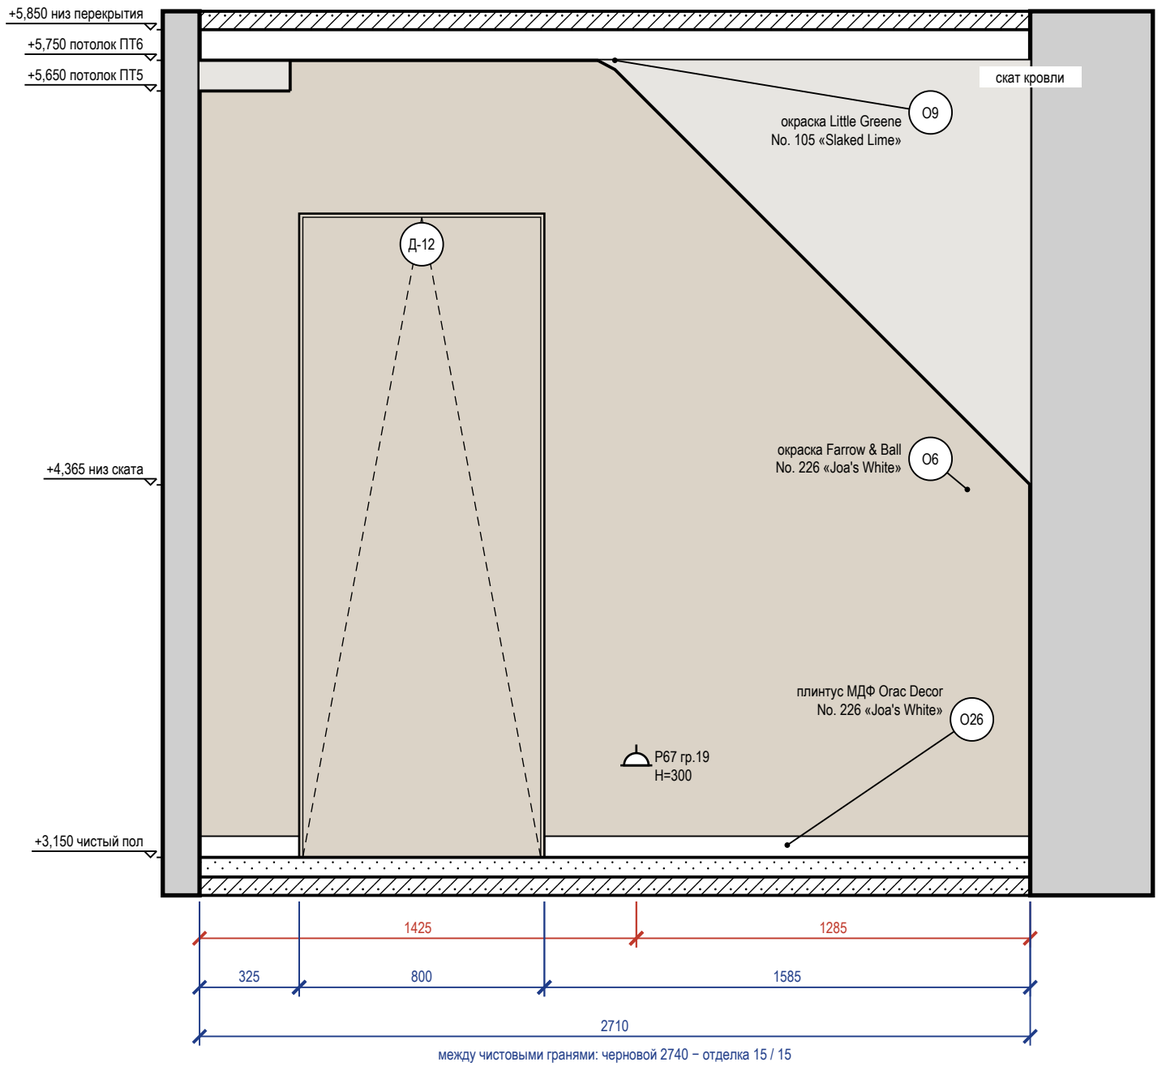


Схема развёрток (М 1:100)

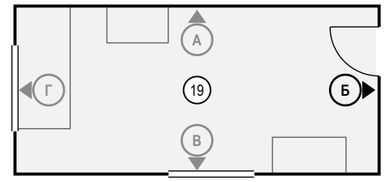

Ведомость отделки (на листе)

Марка	Поверхность	Материал, изделие	Цвет, код	Кол.
О6	стены	окраска, Farrow & Ball Modern Emulsion, матовая, подготовка Q3	Farrow & Ball No. 226 «Joa's White»	5,4 м²
О9	потолок	окраска, Little Greene Absolute Matt, глубокоматовая, подготовка Q3	Little Greene No. 105 «Slaked Lime»	16,3 м²
О26	плинтус	плинтус МДФ, Orac Decor Contour (Luxxus), h 69 мм, SX165	Farrow & Ball No. 226 «Joa's White»	1,9 м

Примечания

1. Размеры — в мм от чистовых поверхностей стен; условные обозначения и общие указания — лист 3.
2. Двери скрытого монтажа — полотно в плоскости стены, отделка стены по полотну, плинтус прерывается у короба (узел — на листе узлов).
3. Потолок — у каждой стены свой, по плану потолков (ПТ6, ПТ5); ступени — зоной, кромка короба перед нишей — тонкой линией.

					Проект: Дом 331 м²	М 1:20
	Лист	№ док.	Подпись	Дата		
Дизайнер	Кырлан А.С.			04.11.26	Развёртка стены Б. Спальня 4 (пом. 19)	

Стадия	Лист	Листов
П	138	168

Развёртка стены В


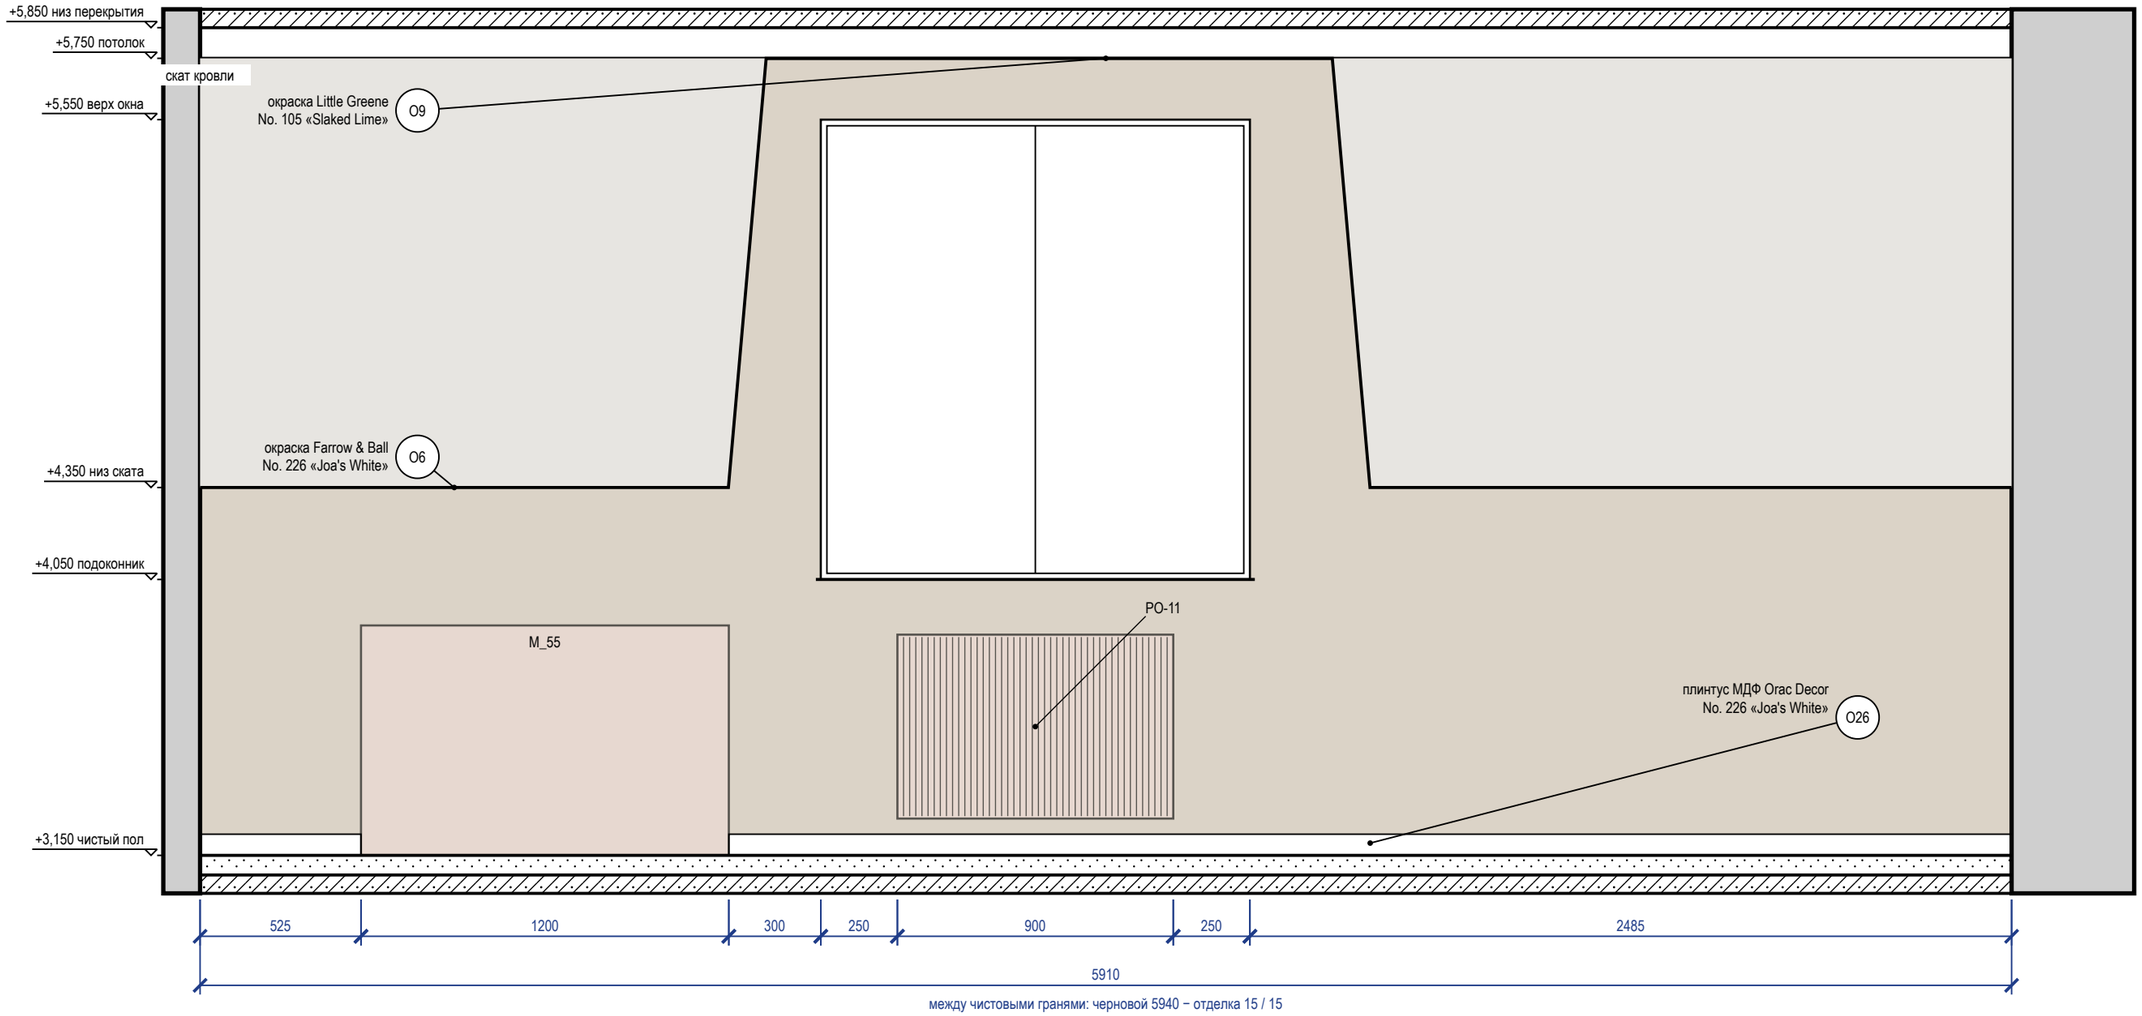


Схема развёрток (М 1:100)

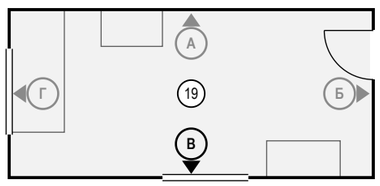

Ведомость отделки (на листе)

Марка	Поверхность	Материал, изделие	Цвет, код	Кол.
O6	стены	окраска, Farrow & Ball Modern Emulsion, матовая, подготовка Q3	Farrow & Ball No. 226 «Joa's White»	13,3 м²
O9	потолок	окраска, Little Greene Absolute Matt, глубокоматовая, подготовка Q3	Little Greene No. 105 «Slaked Lime»	16,3 м²
O26	плинтус	плинтус МДФ, Orac Decor Contour (Luxxus), h 69 мм, SX165	Farrow & Ball No. 226 «Joa's White»	4,7 м

Примечания

1. Размеры — в мм от чистовых поверхностей стен; условные обозначения и общие указания — лист 3.
2. Стена В показана двумя видами: здесь — архитектурная развёртка (мебель, отделка, проёмы, высоты), электроточки и выводы ВК с привязками и таблицей — на листе 140 («Привязки»).
3. Потолок — у каждой стены свой, по плану потолков (ПТ6); ступени — зоной, кромка короба перед нишей — тонкой линией; в поле потолка: ПТ5 +5,650.

					Проект: Дом 331 м² — М 1:20
	Лист	№ док.	Подпись	Дата	Развёртка стены В. Спальня 4 (пом. 19)
Дизайнер	Кырлан А.С.			04.11.26	

Стадия	Лист	Листов
П	139	168

Развёртка стены В: электроточки и выводы

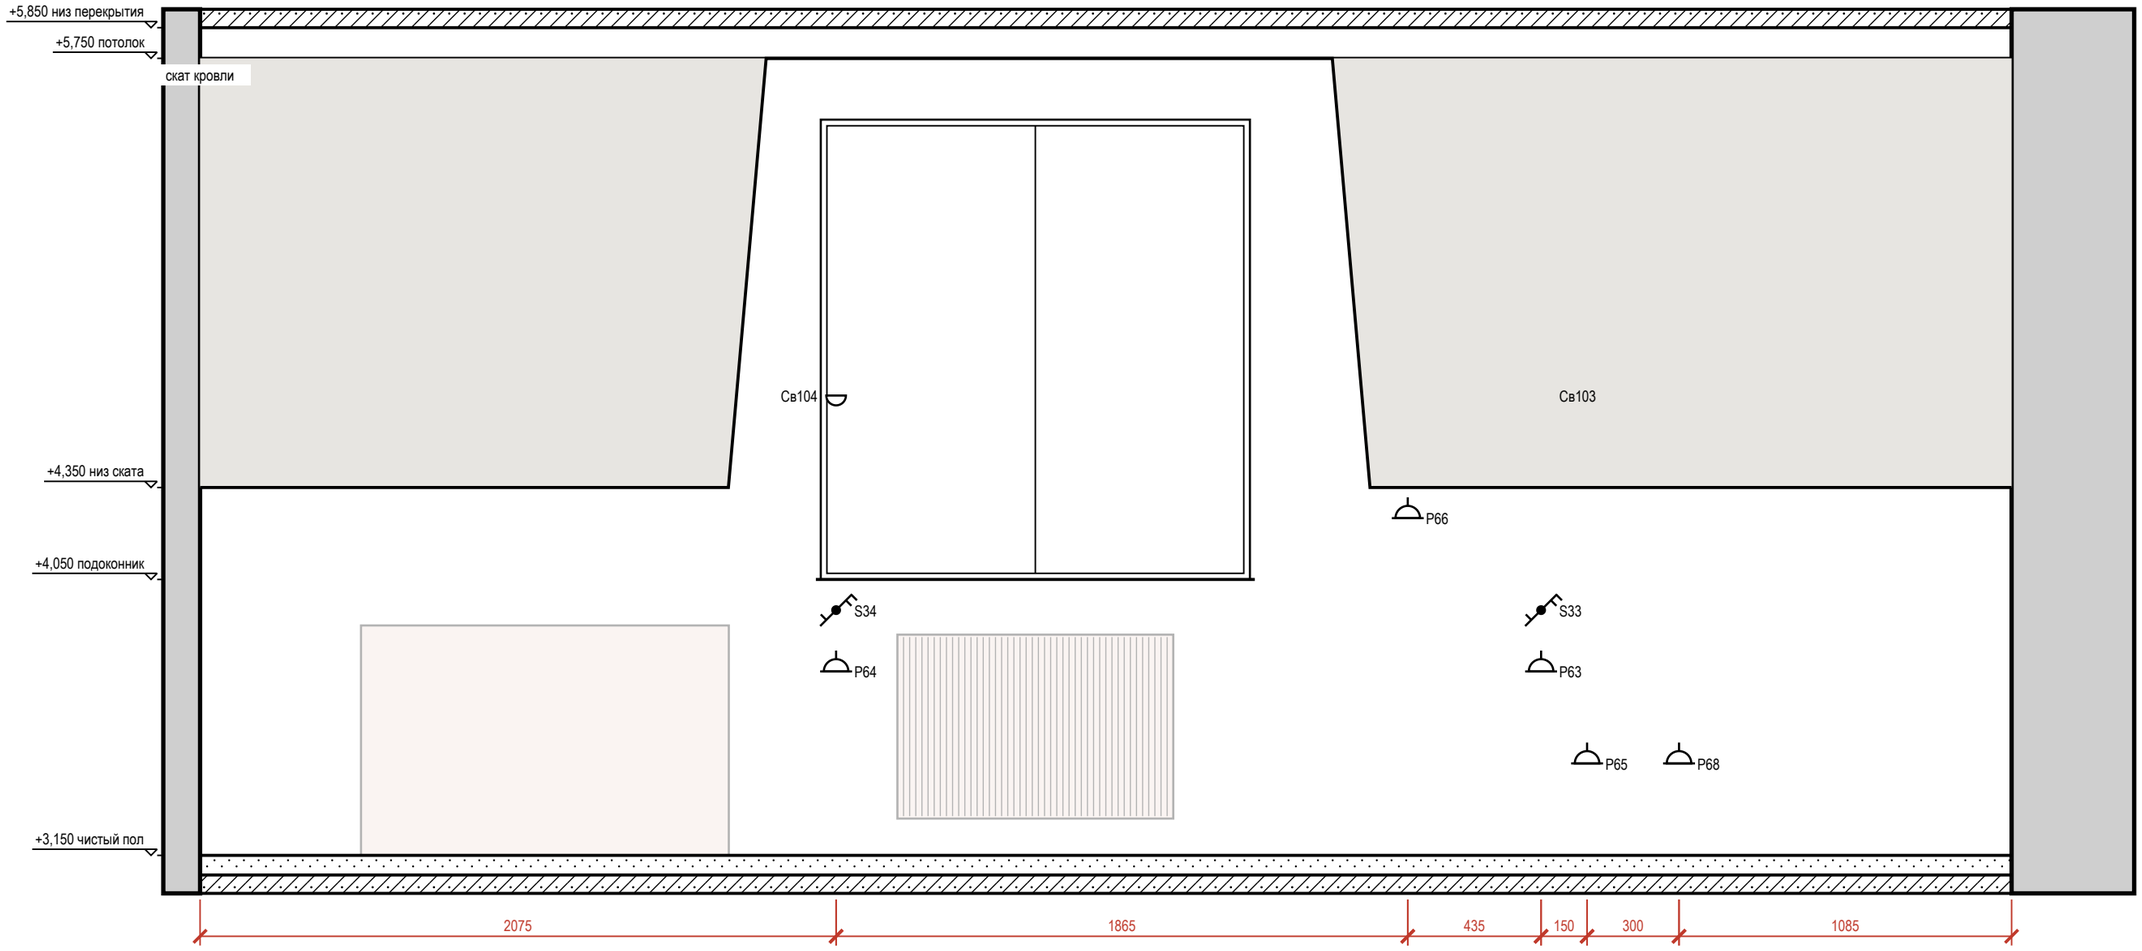



Таблица привязок электроточек и выводов

Марка	Назначение	От угла, мм	Н от пола, мм	Примечание
P64	розетка: у кровати	2075	600	гр. 19
S34	выключатель	2075	800	гр. 1
Св104	светильник настенный	2075	1500	гр. 1
P66	розетка: ТВ над комодом (в одной зоне с ТВ5, LAN6)	3940	1100	гр. 19
P63	розетка: у кровати	4375	600	гр. 19
S33	выключатель	4375	800	гр. 1
Св103	светильник настенный	4375	1500	гр. 1
P65	розетка: у комода	4525	300	гр. 19
P68	розетка: уборка у входа	4825	300	гр. 19

Условные обозначения

- розетка с заземляющим контактом; у знака — марка, ×N постов в рамке, гр. — группа щита, Н — высота оси, мм
- выключатель одноклавишный
- выключатель двухклавишный (флажков — по числу клавиш)
- выключатель с проходной или перекрёстной клавишей (обратный флажок); тип клавиши — в подписи
- светильник настенный (бра), Н — высота оси
- привязки точек и выводов от угла и от пола, мм
- марка развёртки: буква стены, стрелка — взгляд

Схема развёрток (М 1:100)

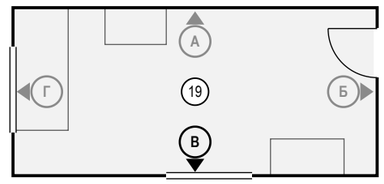

Примечания

1. Вид «Привязки» стены В — электроточки и выводы ВК; архитектурная развёртка (мебель, отделка, проёмы, высоты) — на листе 139. Мебель и приборы — подложкой для ориентира; их марки и обозначения мебели, проёмов и стен — там же.
2. Привязки — в мм: по горизонтали от левого чистового угла стены до оси изделия, Н — от чистого пола до оси; все точки — в таблице привязок. Красная цепочка — привязки по осям; точки ближе 120 мм одна к другой в цепочку не дробятся — их привязки только в таблице.
3. У знака — марка электроточки (Р — розетка, S — выключатель, Св — светильник, ЭВ — вывод кабеля); условные обозначения и общие указания — лист 3.

	Лист	№ док.	Подпись	Дата
Дизайнер	Кырлан А.С.			04.11.26

Проект: Дом 331 м² — М 1:20

Привязки электроточек, стена В. Спальня 4 (пом. 19)

Стадия	Лист	Листов
П	140	168

выпуск 04.11.2026 № f163a372b2 · стр. 140 из 168

Развёртка стены Г


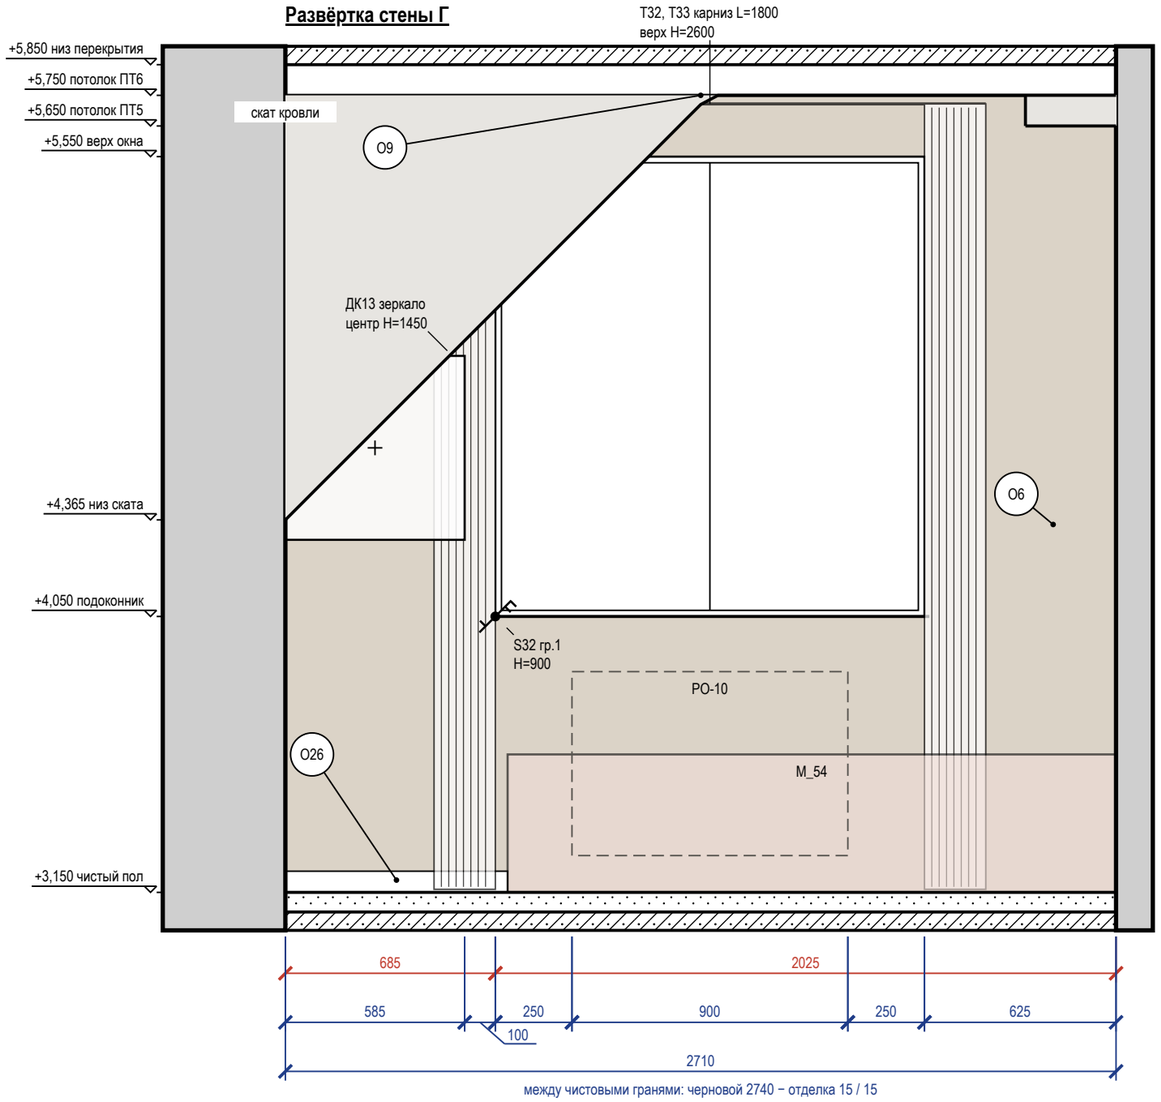


Схема развёрток (М 1:100)

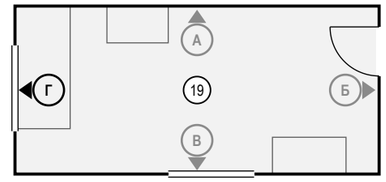

Ведомость отделки (на листе)


Марка	Поверхность	Материал, изделие	Цвет, код	Кол.
О6	стены	окраска, Farrow & Ball Modern Emulsion, матовая, подготовка Q3	Farrow & Ball No. 226 «Joa's White»	4,9 м²
О9	потолок	окраска, Little Greene Absolute Matt, глубокоматовая, подготовка Q3	Little Greene No. 105 «Slaked Lime»	16,3 м²
О26	плинтус	плинтус МДФ, Orac Decor Contour (Luxxus), h 69 мм, SX165	Farrow & Ball No. 226 «Joa's White»	0,7 м

Примечания

1. Размеры — в мм от чистовых поверхностей стен; условные обозначения и общие указания — лист 3.
2. Картины и зеркала крепить к основанию по паспорту изделия (закладные и анкеры — в перечне скрытых работ); крест — ось центра предмета.
3. Карнизы (шины) — по ведомости текстиля декоратора: длина L и верх H на развёртке — те же числа, что в ведомости; крепление — до окраски потолка.
4. Потолок — у каждой стены свой, по плану потолков (ПТ6, ПТ5); ступени — зоной, кромка короба перед нишей — тонкой линией.

					Проект: Дом 331 м²	М 1:20
	Лист	№ док.	Подпись	Дата	Развёртка стены Г. Спальня 4 (пом. 19)	Стадия / Лист / Листов
Дизайнер	Кырлан А.С.			04.11.26		П / 141 / 168

Развёртка стены А

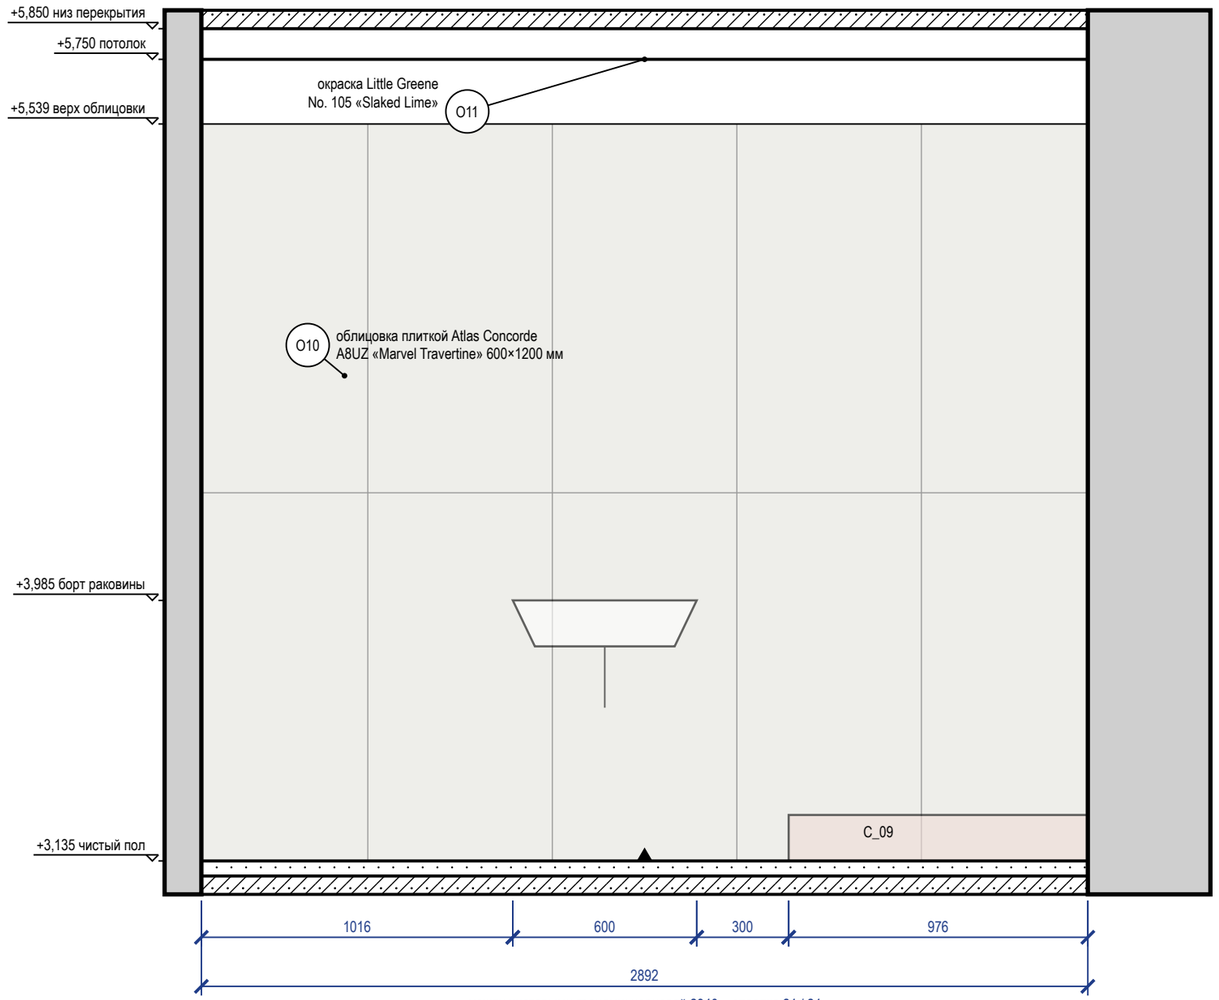

Развёртка стены Б


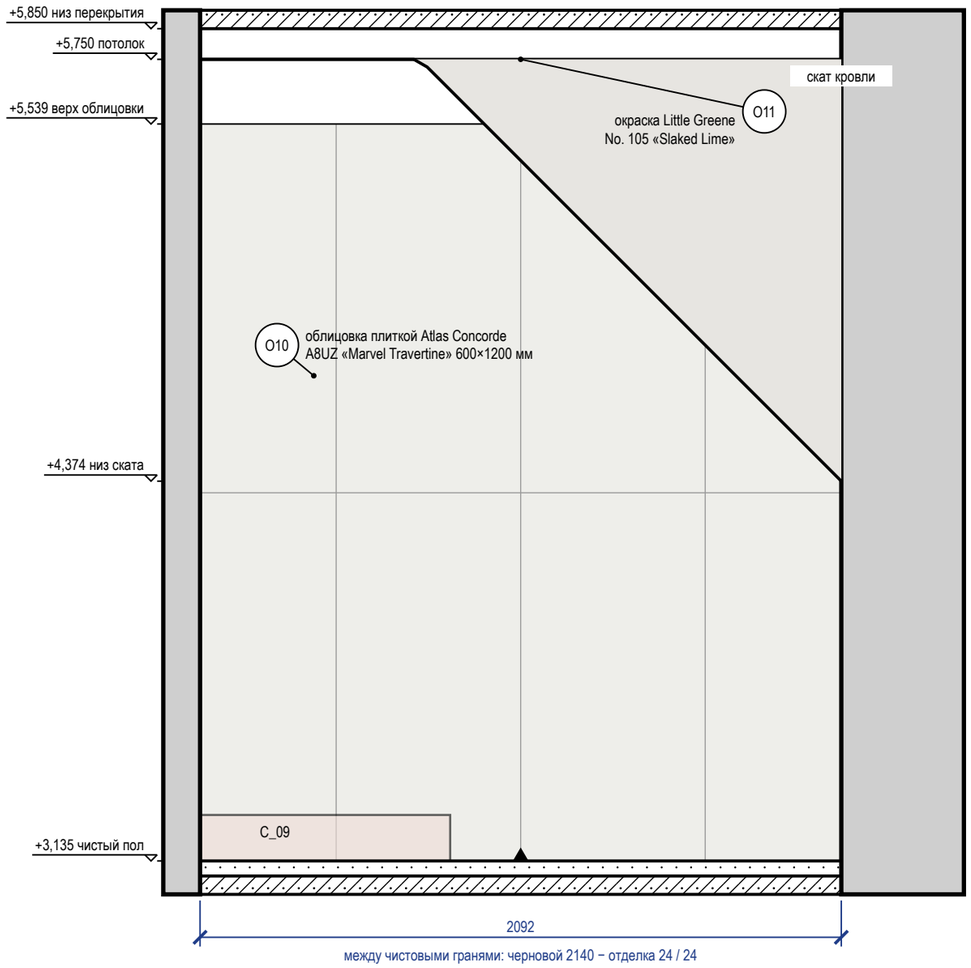


Схема развёрток (М 1:100)

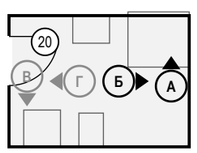

Ведомость отделки (на листе)


Марка	Поверхность	Материал, изделие	Цвет, код	Кол.
О10	стены	облицовка плиткой, Atlas Concorde Marvel Travertine, 600×1200×9 мм, A8UZ, затирка CG2WA	Atlas Concorde A8UZ «Marvel Travertine»	12 м²
О11	потолок	окраска, Little Greene Intelligent Bathroom, матовая, подготовка Q3	Little Greene No. 105 «Slaked Lime»	6,3 м²

Примечания

1. Размеры — в мм от чистовых поверхностей стен; условные обозначения и общие указания — лист 3.
2. Стены А, Б показаны двумя видами: здесь — архитектурная развёртка (мебель, отделка, проёмы, высоты), электроточки и выводы ВК с привязками и таблицей — на листе 143 («Привязки»).
3. Схема мебели, приборов и декора не является технической документацией для производства мебели; габариты — по паспортам изделий.
4. Облицовка — по сетке швов 2 мм, раскладка от оси стены (треугольник у пола), целые ряды от пола; подрезки — по листу раскладки плитки.
5. Гидроизоляция в 2 слоя, заход на стены 200 мм; у душа — до 2000 и 500 мм за поддон — до облицовки, с актом скрытых работ и тестом проливом (узел — на листе узлов).

					Проект: Дом 331 м²	М 1:20
	Лист	№ док.	Подпись	Дата		
Дизайнер	Кырлан А.С.			04.11.26	Развёртки стен А, Б. Санузел 2 (пом. 20)	
					Стадия: П	Лист: 142 / Листов: 168

Развёртка стены А: электроточки и выводы

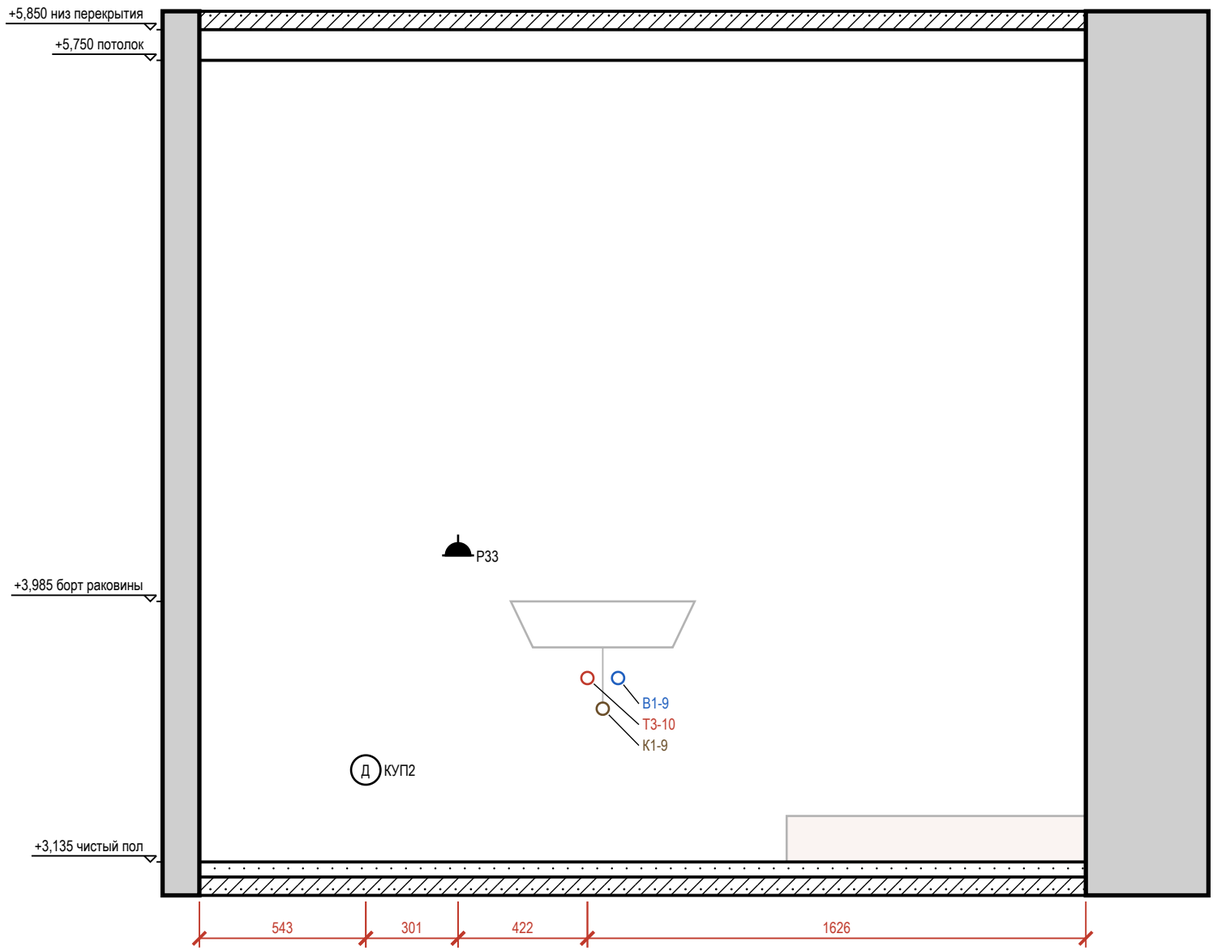

Развёртка стены Б: электроточки и выводы

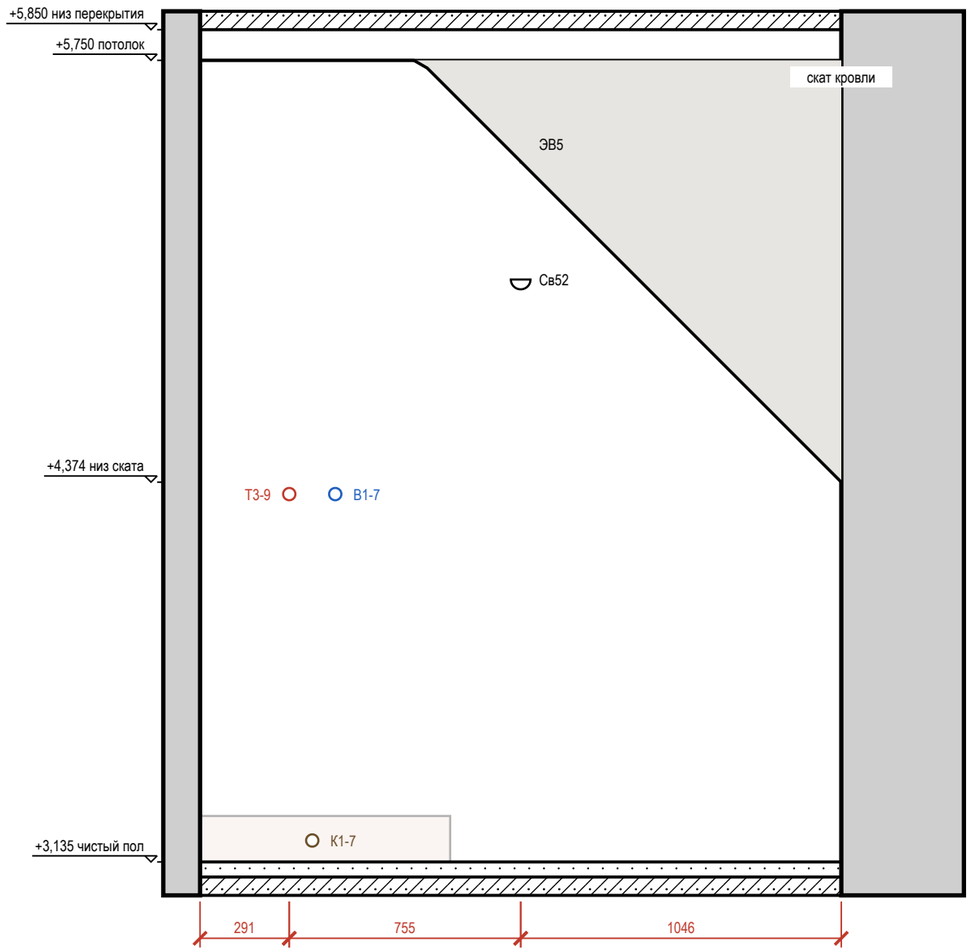


Таблица привязок электроточек и выводов

Стена	Марка	Назначение	От угла, мм	Н от пола, мм	Примечание
А	КУП2	КУП — уравнивание потенциалов (ДСУП)	543	300	
А	Р33	розетка: фен у умывальника	844	1000	гр. 13, IP44
А	Т3-10	горячая вода — умывальник	1266	600	межос. 100
А	К1-9	канализация — умывальник	1316	500	Ø50
А	В1-9	холодная вода — умывальник	1366	600	межос. 100

Стена	Марка	Назначение	От угла, мм	Н от пола, мм	Примечание
Б	Т3-9	горячая вода — душ	291	1200	межос. 150
Б	К1-7	канализация — душ	366	70	Ø50; сифон поддона
Б	В1-7	холодная вода — душ	441	1200	межос. 150
Б	Св52	светильник настенный	1046	1900	гр. 3
Б	ЭВ5	вывод кабеля: вентилятор ВР3 (таймер выбега)	1046	2343	гр. 3

Условные обозначения

- розетка влагозащищённая IP44
- вывод кабеля для подключения прибора (без розетки), марка ЭВ
- светильник настенный (бра), Н — высота оси
- вывод В1 (код — в ведомости привязок)
- вывод Т3 (код — в ведомости привязок)
- вывод К1 (код — в ведомости привязок)
- привязки точек и выводов от угла и от пола, мм

Примечания

1. Вид «Привязки» стен А, Б — электроточки и выводы ВК; архитектурная развёртка (мебель, отделка, проёмы, высоты) — на листе 142. Мебель и приборы — подложкой для ориентира; их марки и обозначения мебели, проёмов и стен — там же.
2. Привязки — в мм: по горизонтали от левого чистового угла стены до оси изделия, Н — от чистого пола до оси; все точки — в таблице привязок. Красная цепочка — привязки по осям; точки ближе 120 мм одна к другой в цепочку не дробятся — их привязки только в таблице.
3. У знака — марка электроточки (Р — розетка, S — выключатель, Св — светильник, ЭВ — вывод кабеля); условные обозначения и общие указания — лист 3.
4. Коды выводов ВК: В1 — холодная вода, Т3 — горячая вода, К1 — канализация; номер после дефиса — номер вывода на листе выводов сантехники.

	Лист	№ док.	Подпись	Дата
Дизайнер	Кырлан А.С.			04.11.26


Проект: Дом 331 м² — М 1:20

Привязки электроточек и выводов ВК, стены А, Б. Санузел 2 (пом. 20)

Стадия	Лист	Листов
П	143	168


выпуск 04.11.2026 № f163a372b2 · стр. 143 из 168

Развёртка стены В

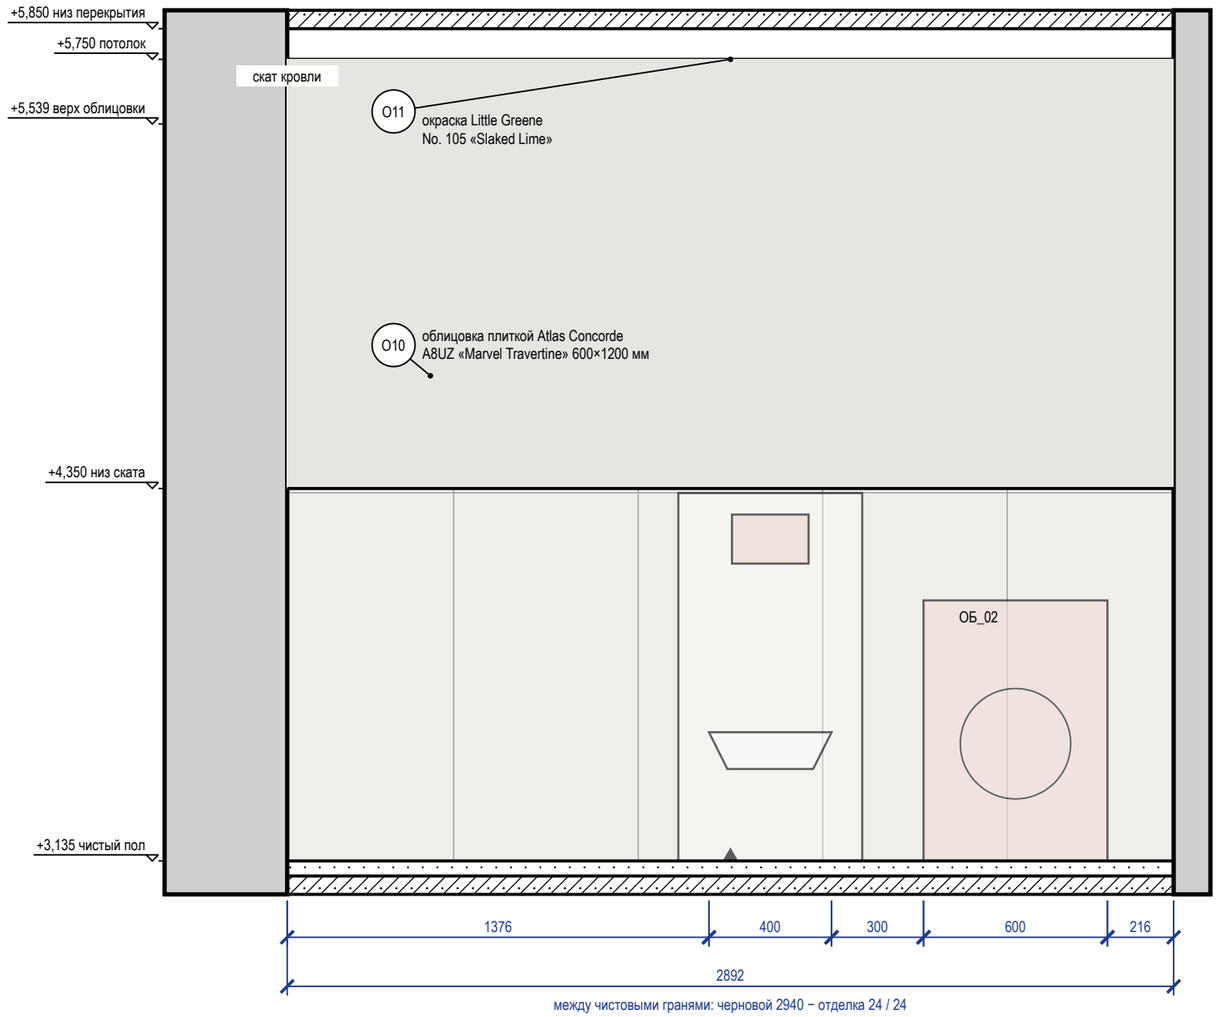


между чистовыми гранями: черновой 2940 − отделка 24 / 24

Развёртка стены Г

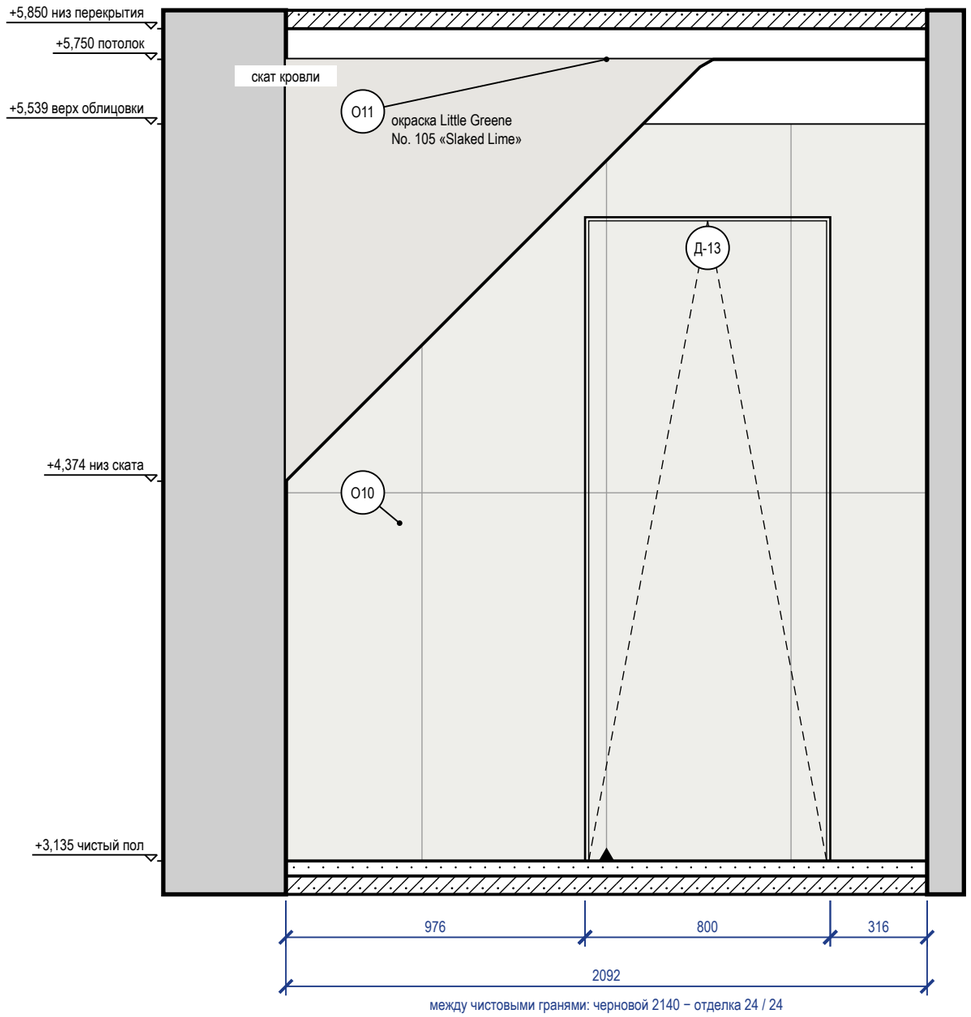

между чистовыми гранями: черновой 2140 − отделка 24 / 24

Схема развёрток (М 1:100)

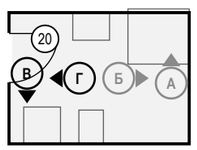

Ведомость отделки (на листе)

Марка	Поверхность	Материал, изделие	Цвет, код	Кол.
О10	стены	облицовка плиткой, Atlas Concorde Marvel Travertine, 600×1200×9 мм, A8UZ, затирка CG2WA	Atlas Concorde A8UZ «Marvel Travertine»	10,3 м²
О11	потолок	окраска, Little Greene Intelligent Bathroom, матовая, подготовка Q3	Little Greene No. 105 «Slaked Lime»	6,3 м²

Примечания

1. Размеры — в мм от чистовых поверхностей стен; условные обозначения и общие указания — лист 3.
2. Стена В показана двумя видами: здесь — архитектурная развёртка (мебель, отделка, проёмы, высоты), электроточки и выводы ВК с привязками и таблицей — на листе 145 («Привязки»).
3. Схема мебели, приборов и декора не является технической документацией для производства мебели; габариты — по паспортам изделий.
4. Облицовка — по сетке швов 2 мм, раскладка от оси стены (треугольник у пола), целые ряды от пола; подрезки — по листу раскладки плитки.
5. Гидроизоляция в 2 слоя, заход на стены 200 мм; у душа — до 2000 и 500 мм за поддон — до облицовки, с актом скрытых работ и тестом проливом (узел — на листе узлов).
6. Двери скрытого монтажа — полотно в плоскости стены, отделка стены по полотну, плинтус прерывается у короба (узел — на листе узлов).

					Проект: Дом 331 м² — М 1:20
	Лист	№ док.	Подпись	Дата	
Дизайнер	Кырлан А.С.			04.11.26	Развёртки стен В, Г. Санузел 2 (пом. 20)

Стадия	Лист	Листов
П	144	168

Развёртка стены В: электроточки и выводы

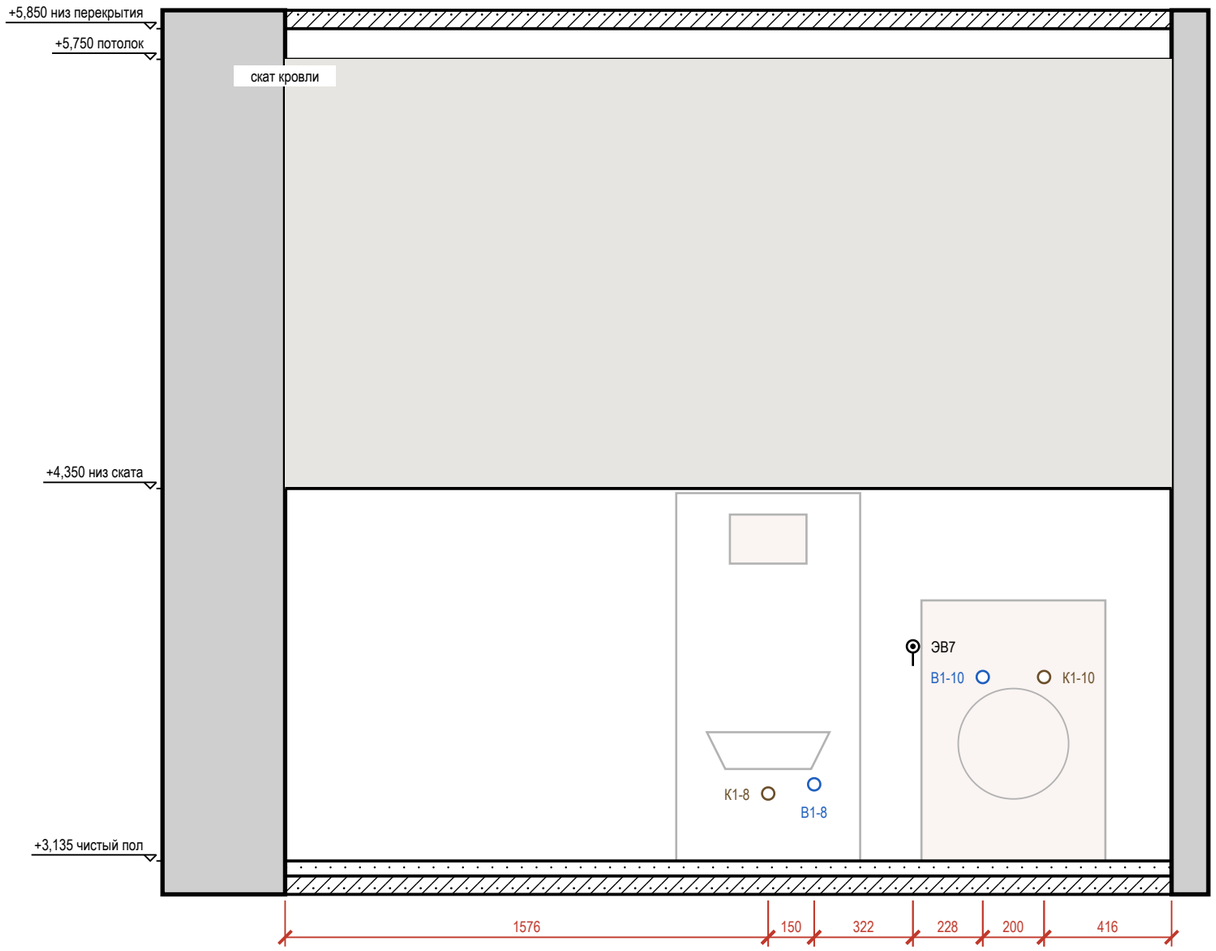



Таблица привязок электроточек и выводов

Марка	Назначение	От угла, мм	Н от пола, мм	Примечание
К1-8	канализация — унитаз подвесной	1576	220	Ø110
В1-8	холодная вода — унитаз подвесной	1726	250	в раме инсталляции
ЭВ7	вывод кабеля: полотенцесушитель П13	2048	700	гр. 13
В1-10	холодная вода — стиральная машина	2276	600	кран машины
К1-10	канализация — стиральная машина	2476	600	Ø50

Условные обозначения

- вывод кабеля для подключения прибора (без розетки), марка ЭВ
- вывод В1 (код — в ведомости привязок)
- вывод К1 (код — в ведомости привязок)
- привязки точек и выводов от угла и от пола, мм
- (А) марка развёртки: буква стены, стрелка — взгляд

Схема развёрток (М 1:50)

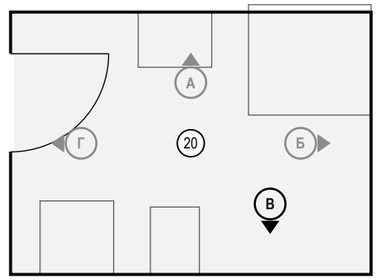

Примечания

1. Вид «Привязки» стены В — электроточки и выводы ВК; архитектурная развёртка (мебель, отделка, проёмы, высоты) — на листе 144. Мебель и приборы — подложкой для ориентира; их марки и обозначения мебели, проёмов и стен — там же.
2. Привязки — в мм: по горизонтали от левого чистового угла стены до оси изделия, Н — от чистого пола до оси; все точки — в таблице привязок. Красная цепочка — привязки по осям; точки ближе 120 мм одна к другой в цепочку не дробятся — их привязки только в таблице.
3. У знака — марка электроточки (Р — розетка, S — выключатель, Св — светильник, ЭВ — вывод кабеля); условные обозначения и общие указания — лист 3.
4. Коды выводов ВК: В1 — холодная вода, Т3 — горячая вода, К1 — канализация; номер после дефиса — номер вывода на листе выводов сантехники.

	Лист	№ док.	Подпись	Дата
Дизайнер	Кырлан А.С.			04.11.26

Проект: Дом 331 м² — **М 1:20**

Привязки электроточек и выводов ВК, стена В. Санузел 2 (пом. 20)

Стадия	Лист	Листов
П	145	168

Комплект предварительный по пунктам этих таблиц. Пока по пункту нет ответа или решения, показанное на указанном листе — допущение проектировщика, а не утверждённое решение.
Сводка: открытых вопросов — 12 (из них ждут факта объекта — 7: контрольного обмера, обследования или документа); конфликтов между разделами — 1; изменений в реестре — 2, из них без подписи — 2.

Открытые вопросы и принятые допущения

№	Формулировка	Вид	Кто решает	Если решения нет	Лист, где это проявляется
К-1	Размеры дома на картинке заказчика (470 px) не читаются: состав помещений и форма сняты с картинки, размеры подобраны проектировщиком под площади этажей 185,80 и 145,73 м². Нужен исходный проект дома (АР) или обмер.	Отсутствует Ждёт: обмера	Архитектор-планировщик	размеры на листах — предложение проектировщика; мебель на заказ и материалы по ним не заказывать	л. 6, 7 — План планировки от заказчика л. 6, 8, 13, 17, 25, 27, 33, 34, 40, 43, 48, 59, 61, 63, 67, 69, 71, 73, 87–89 — 1-й этаж л. 17, 18 — План размещения мебели и оборудования
К-2	Высоты этажей и кровля не известны: приняты 2800 мм (1-й этаж) и 2700 мм (горизонтальная часть потолка мансарды); скаты двускатная кровля, конёк вдоль длинной стороны, колено 1200 мм, уклон 45° (по перспективе и фасаду с картинки).	Отсутствует	Архитектор-планировщик	высоты — принятые, уточнить по проекту АР	л. 6, 7 — План планировки от заказчика л. 6, 8, 13, 17, 25, 27, 33, 34, 40, 43, 48, 59, 61, 63, 67, 69, 71, 73, 87–89 — 1-й этаж л. 48, 49 — План потолков
К-4	Разрешённая мощность дома по ТУ неизвестна, принята 15 кВт.	Отсутствует	Инженер-электрик	щит и группы рассчитаны на 15 кВт; при меньших ТУ пересчёт	л. 57 — Однолинейная схема щита л. 59, 60 — План розеток и электровыводов л. 6, 8, 13, 17, 25, 27, 33, 34, 40, 43, 48, 59, 61, 63, 67, 69, 71, 73, 87–89 — 1-й этаж
К-5	Планировка этажей — предложение проектировщика по составу помещений с картинки (несущие стены, лестница, перекрытие не известны): нужен проект АР/КР дома.	Отсутствует Ждёт: документа	Архитектор-планировщик	перегородки и проёмы — предложение, к строительству не выдаются	л. 6, 7 — План планировки от заказчика л. 6, 8, 13, 17, 25, 27, 33, 34, 40, 43, 48, 59, 61, 63, 67, 69, 71, 73, 87–89 — 1-й этаж
К-6	Лестница Л-1 на картинке заказчика — одномаршевая в холле 1-го этажа (3,0×3,6 м), видно 11 проступей. До пола мансарды +3,150 нужно 18 подъёмов по 175 мм (равные ступени — СП 55.13330.2016 п. 8.2), то есть 17 проступей по 280 мм = 4,76 м длины марша; в холл 3,48 м в свету одномаршевая не встаёт (не хватает 1,66 м). Варианты: Г-образная с 3 забежными ступенями (8 + 3 + 6 подъёмов по 175 — встаёт в холл 3,24×2,68 м; при детях забежные — компромисс), Г-образная с площадкой (9 + 7 подъёмов по 197 мм — круче практики 150–180, для дома допустимо: уклон не нормируется, СП 55 п. 7.5), перенос лестницы или иная высота этажа по проекту АР/КР. Нужны: решение по типу марша и проект АР/КР (высота этажа, перекрытие, проём). На плане 1-го этажа марш по картинке стоит вдоль стены холла с проёмом Пр-2 из гостиной и перекрывает его: в любом варианте Пр-2 освободить (сдвинуть проём или марш); на монтажных планах обоих этажей марш и проём перекрытия показаны по принятому габариту до решения.	Отсутствует Ждёт: обмера, затем решения	Архитектор-планировщик	марш на планах и лист «Лестница Л-1» — по картинке (11 проступей, до отм. +2,100), ограждение и проём считаются по этому габариту; изделие не заказывать, проём в перекрытии не резать	architect/stairs-л-1
К-7	Климатический подрайон (СП 131.13330) не задан: принят не северный — жилые комнаты и кухня под потолком от 2,5 м (СП 54, п. 5.12); в IA, IБ, IГ, IД, IVA — от 2,7 м.	Отсутствует Ждёт: документа	Архитектор-планировщик	отметки потолков жилых — по 2,5 м; при северном подрайоне уровни ниже 2,7 м пересчитать до заказа каркаса	л. 48, 49 — План потолков л. 6, 8, 13, 17, 25, 27, 33, 34, 40, 43, 48, 59, 61, 63, 67, 69, 71, 73, 87–89 — 1-й этаж
К-8	Душ С_01 с трапом (санузел 1-го этажа): в стяжке 35 мм трап не встаёт — монтажная высота трапа ≈ 90 мм (по паспорту модели) + уклон отвода Ø50 до стояка Ст К1-1 (1,70 м × 25 мм/м = 42 мм) = 132 мм. Предложение проектировщика: душевая зона у стены Б под стояками (не на них), подиум 1190 × 900 высотой 100 мм (гидроизоляция по плите под подиумом и по подиуму, весь санузел; узел 1 на схеме разводки). Альтернативы: пол 1-го этажа по грунту или перекрытию с пирогом ≥ 132 мм по проекту АР/КР (тогда без подиума), низкий поддон на ножках.	Спорно Ждёт: документа, затем решения	Инженер ВК (вода, канализация)	трап и подиум не выполнять, пол санузла до решения не стяжать	л. 25, 26 — План выводов сантехники л. 6, 8, 13, 17, 25, 27, 33, 34, 40, 43, 48, 59, 61, 63, 67, 69, 71, 73, 87–89 — 1-й этаж л. 27, 28 — Схема разводки водопровода и канализации л. 73, 74 — План покрытий пола
К-9	Дверь Д-4 гостиной (пом. 5) на террасу, проём 2400 × 2100, остеклённая: число полотен и ширина полотна в данных не заданы (ряд полотен — до 1200 мм), толщина и класс безопасного стекла тоже. Одним полотном 2400 мм дверь при открывании на 90° задевает диван М_18, такое полотно не изготовить. Решить: двупольная 2 × 1150 (сектор полотна 1150 до дивана не доходит), раздвижная или портальная система; стекло — закалённое или многослойное, толщина и класс — по выбору системы (передать стекольщику).	Отсутствует Ждёт: решения	Архитектор-планировщик	Д-4 остаётся проёмом без заданного полотна: дверь не заказать, зона открывания на плане мебели — по ширине проёма	л. 43, 44 — План размещения дверей л. 6, 8, 13, 17, 25, 27, 33, 34, 40, 43, 48, 59, 61, 63, 67, 69, 71, 73, 87–89 — 1-й этаж л. 17, 18 — План размещения мебели и оборудования
К-10	Кухня-столовая (пом. 1): мойка М_01 и модули М_06, М_02 стоят под окном 1400 × 1500 стены А с низом проёма +0,900 подоконник в уровне столешницы (+0,900). Смеситель мойки упирается в створку, открывающуюся внутрь, примыкание столешницы к откосу и подоконнику не решено. Выбрать: створка над мойкой глухая или поворотно-откидная с ограничителем, подоконник поднять (низ проёма от +1,050) или столешница заходит в проём вместо подоконника.	Решение Ждёт: решения	Дизайнер интерьера	столешница у окна не раскраивается, мойка М_01 и смеситель не заказываются; монтажная схема кухни показывает проём и конфликт	л. 10 — Кухня (пом. 1). Монтажная схема
К-11	Тип котла (газ / электро / твёрдое топливо) и его мощность не выбраны. От них зависят воздухообмен и приток котельной (пом. 4; при газе — СП 62.13330, дымоход), вытяжка гаража (пом. 10) наружу своим каналом и разводка отопления от коллектора. Выбрать котёл.	Решение	Инженер ОВ	котельная и гараж без устройств вентиляции; разводка отопления — принципиальная	л. 71, 72 — План отопления л. 6, 8, 13, 17, 25, 27, 33, 34, 40, 43, 48, 59, 61, 63, 67, 69, 71, 73, 87–89 — 1-й этаж л. 69, 70 — План вентиляции

выпуск 04.11.2026 № f163a372b2 · стр. 146 из 168

					Проект: Дом 331 м²
	Лист	№ док.	Подпись	Дата	Открытые вопросы, принятые допущения и конфликты. Лист 1 из 2
Дизайнер	Кырлан А.С.			04.11.26	

Стадия	Лист	Листов
П	146	168

Открытые вопросы и принятые допущения (продолжение)

№	Формулировка	Вид	Кто решает	Если решения нет	Лист, где это проявляется
К-12	Вентканалы ВК-1…ВК-3 приняты проектировщиком (на картинке заказчика не показаны). У санузла мансарды (пом. 20) канала нет: вытяжка ВР4 — воздуховодом ≈ 6 м до ВК-3. Нужен канал или шахта у санузла (проект дома / решение) либо подтверждение воздуховода с вентилятором по напору.	Отсутствует Ждёт: обмера	Инженер ОВ	вытяжка санузла мансарды — вентилятором с обратным клапаном и воздуховодом под потолком до ВК-3	л. 69, 70 — План вентиляции л. 6, 8, 13, 17, 25, 27, 33, 34, 40, 43, 48, 59, 61, 63, 67, 69, 71, 73, 87–89 — 1-й этаж
К-13	Веранда (пом. 11) и крыльцо (пом. 12): чистый пол −0,030, пирог 140 мм (утеплитель XPS 100, сборное основание ГВЛВ 25, клей 5, керамогранит 10) — верх плиты принят −0,170, то есть своя плита на 106 мм ниже плиты дома (−0,064). Отметка и конструкция плиты веранды и крыльца не известны: проект КР не передан (К-5). Подтвердить по проекту КР или обмером; если плита в уровне дома — пирог свести к 34 мм.	Отсутствует Ждёт: обмера	Архитектор-планировщик	плита веранды и крыльца — на отметке −0,170 (по пирогу); утеплитель и основание не заказывать до подтверждения отметки	л. 73, 74 — План покрытий пола л. 6, 8, 13, 17, 25, 27, 33, 34, 40, 43, 48, 59, 61, 63, 67, 69, 71, 73, 87–89 — 1-й этаж л. 6, 7 — План планировки от заказчика

Конфликты между разделами

№	Формулировка	Разделы	Статус	Кто решает	Если решения нет	Лист, где это проявляется
Кф-1	Кухня-столовая (пом. 1): радиатор РО-1 под окном стены А (800…2200, выведен листом ОВ по оси окна) попадает в объём нижних модулей М_06 (300…1100), М_01 (мойка, 1100…1900) и М_02 (посудомоечная, 1900…2500) — те же модули, что в К-10 (подоконник в уровне столешницы). Экран в модуле невозможен. Решение ОВ: перенос прибора на свободную стену (Г, у окна 1200…2800) или внутрипольный конвектор у окна; либо дизайнер меняет состав ряда у окна. Решение исполнителя (ИЗ-2, 02.11.2026, на утверждение автора): РО-1 перенесён на свободный участок стены Г у угла со стеной В (привязка 3500, 600 × 600, низ +120); ряд под окном А без прибора. Конфликт закрывается подписью ИЗ-2.	ОВ; мебель	У владельца раздела, круг 3	Инженер ОВ	до подписи ИЗ-2 модули М_06, М_01, М_02 и подводки к РО-1 не выполнять	л. 71, 72 — План отопления л. 6, 8, 13, 17, 25, 27, 33, 34, 40, 43, 48, 59, 61, 63, 67, 69, 71, 73, 87–89 — 1-й этаж л. 24 — Ведомости изделий, техники и фурнитуры л. 17, 18 — План размещения мебели и оборудования

Изменения проекта после выпуска листов (реестр изменений)

№	Дата	Лист	Было	Стало	Кто решил, подпись
ИЗ-1	30.10.2026	л. 67, 68 — Управление светильниками л. 6, 8, 13, 17, 25, 27, 33, 34, 40, 43, 48, 59, 61, 63, 67, 69, 71, 73, 87–89 — 1-й этаж л. 63, 64 — План освещения	Линия L17 объединяла светильники веранды (Св59), крыльца (Св60) и санузла 2 мансарды (Св50, Св51, вентилятор В5); единственный выключатель S9 стоял в кухне-столовой; бра Св52 (L18) без выключателя (прим. 8 «назначить управление до монтажа»).	Веранда — линия L12, выключатель S30 в гостиной у двери Д-4; крыльцо — линия L13, выключатель S31 в тамбуре у входной двери; санузел 2 — L17 (свет и вентилятор) и L18 (бра), двухклавишный S32 в холле мансарды у двери Д-13. S9 снят. Конфликт радиатора РО-1 с модулями кухни под окном записан как Кф-1.	Не утверждено: подписи нет. решение исполнителя; на утверждение А. С. Кырлана
ИЗ-2	02.11.2026	л. 71, 72 — План отопления л. 6, 8, 13, 17, 25, 27, 33, 34, 40, 43, 48, 59, 61, 63, 67, 69, 71, 73, 87–89 — 1-й этаж л. 24 — Ведомости изделий, техники и фурнитуры л. 17, 18 — План размещения мебели и оборудования	Радиатор РО-1 выводился листом ОВ под окном стены А кухни-столовой (привязка 1050, 900 × 600) — внутри нижних модулей М_06 (ящики), М_01 (мойка) и М_02 (посудомоечная машина): экран невозможен. Радиаторы дома в данных не были заданы, лист ОВ выводил их сам.	РО-1 — на свободном участке наружной стены Г у угла со стеной В: привязка 3500, 600 × 600, низ +120; ряд под окном А без прибора. Мощность РО-1 + РО-2 сверить теплотехническим расчётом ОВ (котёл и мощность не выбраны, К-11). Все радиаторы дома теперь в данных — одни и те же на листе ОВ, в мебели, DXF и IFC.	Не утверждено: подписи нет. решение исполнителя (ОВ); предложение проектировщика, на утверждение А. С. Кырлана


Примечания

1. Номера листов — по ведомости рабочих чертежей комплекта (лист «Общие данные»).
2. Графа «Если решения нет» показывает состояние решения на листах; влияние на сроки и стоимость по пунктам не оценивалось.
3. Пункт, по которому принято решение, при следующем выпуске комплекта из таблиц исключается.


					Проект: Дом 331 м²
	Лист	№ док.	Подпись	Дата	Открытые вопросы, принятые допущения и конфликты. Лист 2 из 2
Дизайнер	Кырлан А.С.			04.11.26	

Стадия	Лист	Листов
П	147	168


Общий вид

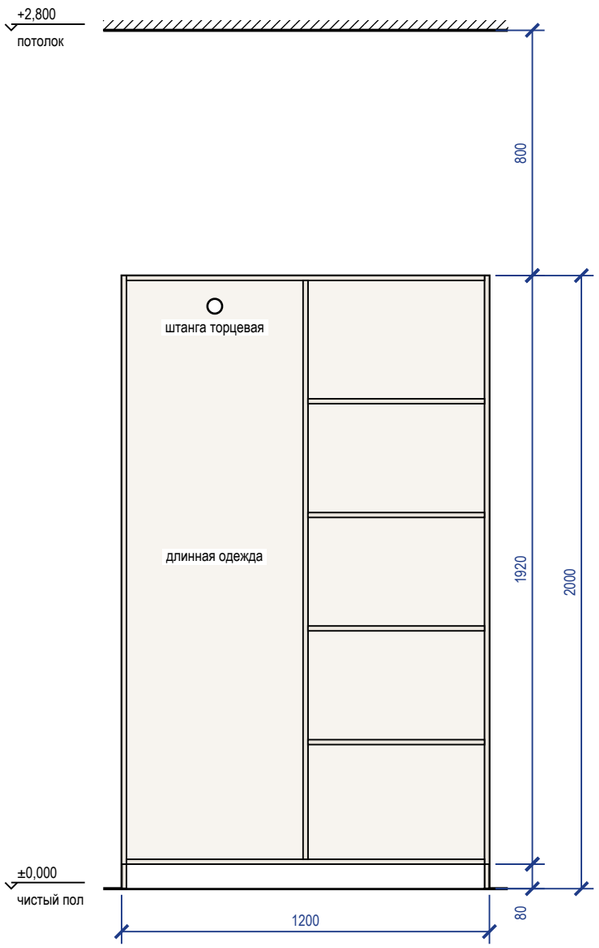


Наполнение, размеры в свету

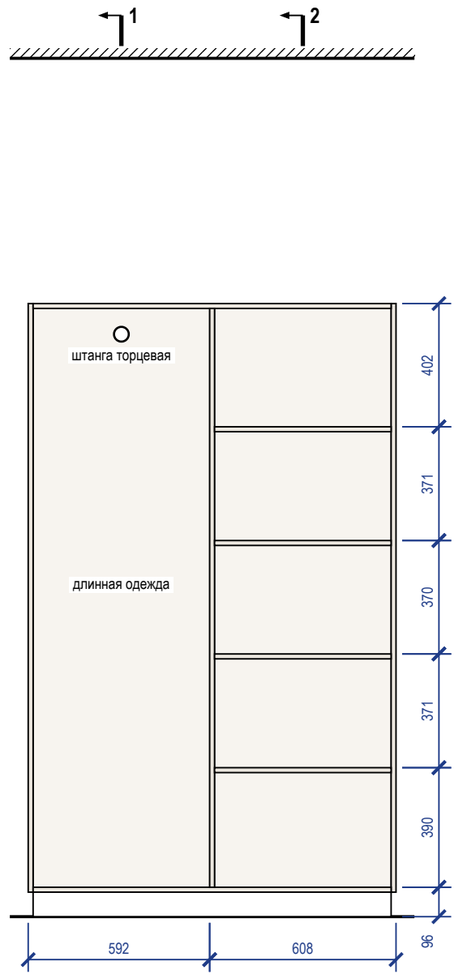

Разрез 1-1

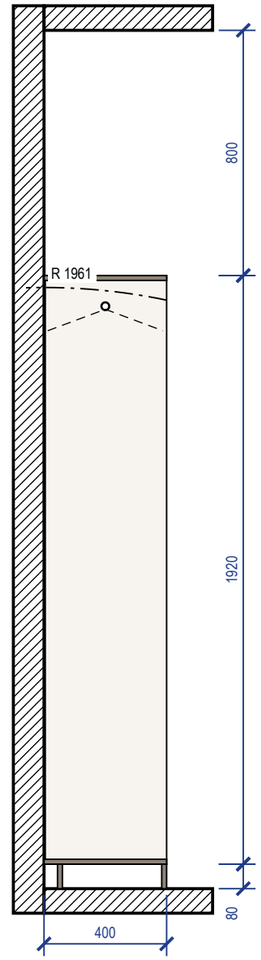


Разрез 2-2

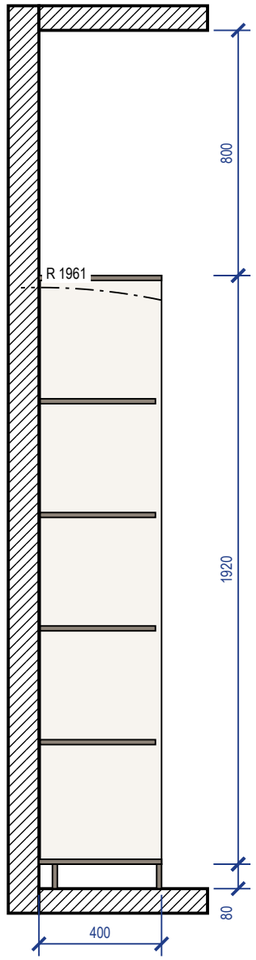

Примечания


1. Размеры — в мм по чистовой отделке; изделие 1200×400×2000 (Ш×Г×В). Перед раскроем — контрольный замер цеха после чистовой отделки стен, пола и потолка.
2. Корпус — ЛДСП 16 мм, задняя стенка ХДФ 4 мм в паз, цоколь 80 мм на регулируемых опорах; открытая система: без фасадов.
3. Кромка: скрытые торцы 0,4 мм, видимые 2 мм (ПВХ/АБС).
4. Присадка по 32-й системе — выполняет цех.
5. Зазор до потолка 800 мм.
6. Подъём корпуса: диагональ боковины без цоколя √(1920² + 400²) = 1961 мм < 2800 мм до потолка — корпус собирается лёжа, поднимается поворотом и ставится на цоколь.
7. Крепление к стене от опрокидывания — уголки 2 шт. к несущему основанию (монтажная схема шкафов).

3D орто

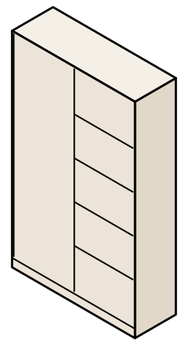


					Проект: Дом 331 м²	**М 1:20**
	Лист	№ док.	Подпись	Дата		
Дизайнер	Кырлан А.С.			04.11.26	Система хранения М_17	Стадия / Лист / Листов
						П / Д_1 / 168


Общий вид

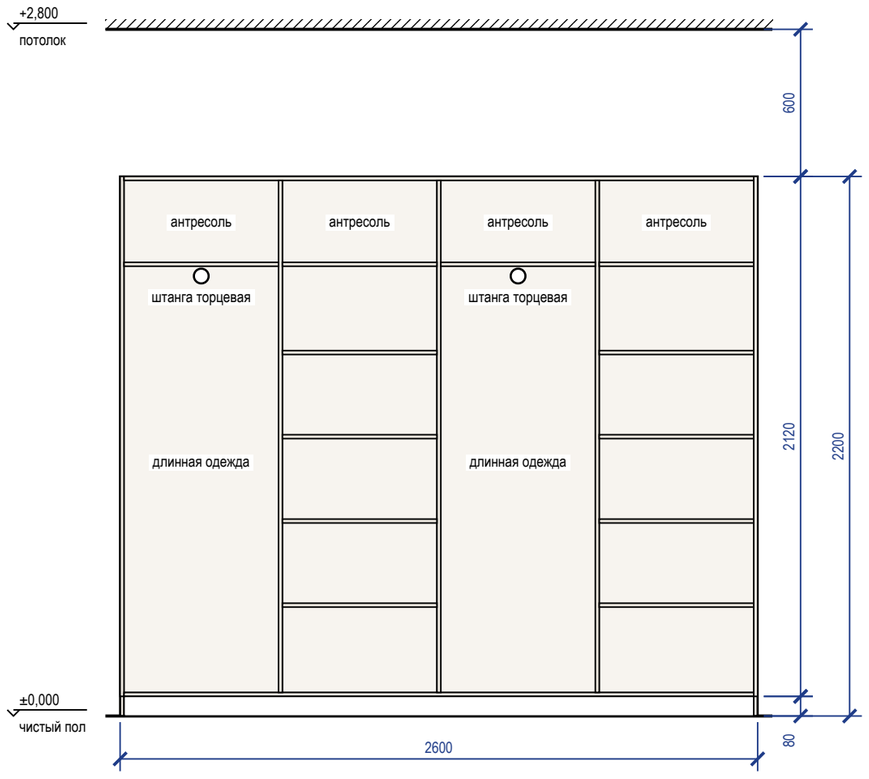


Наполнение, размеры в свету

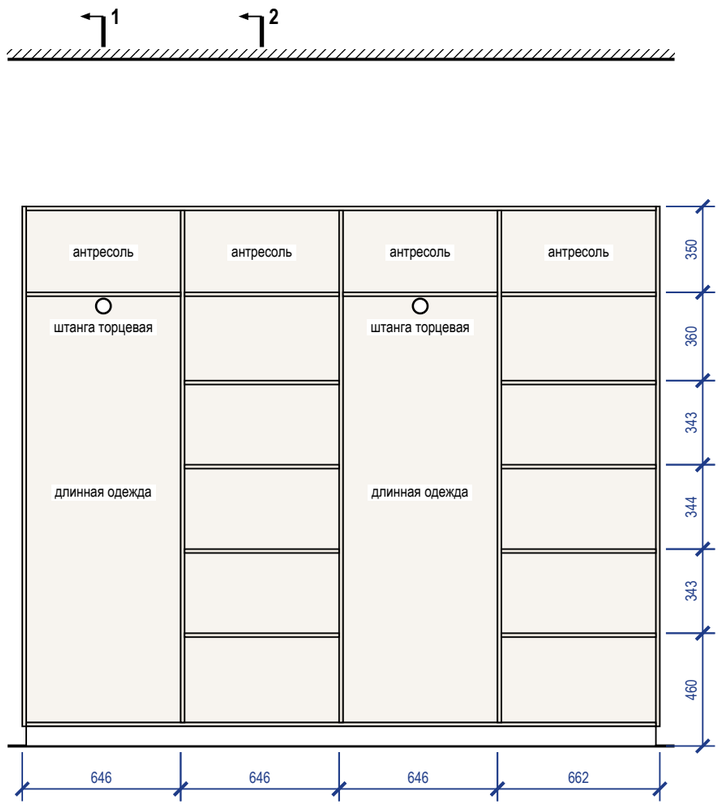

Разрез 1-1

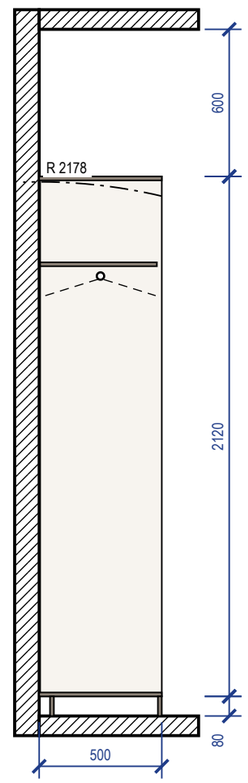


Разрез 2-2

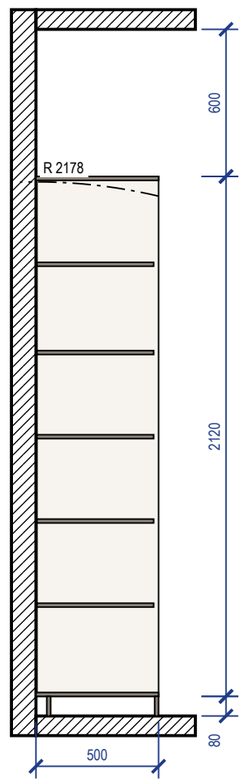

Примечания

1. Размеры — в мм по чистовой отделке; изделие 2600×500×2200 (Ш×Г×В). Перед раскроем — контрольный замер цеха после чистовой отделки стен, пола и потолка.
2. Корпус — ЛДСП 16 мм, задняя стенка ХДФ 4 мм в паз, цоколь 80 мм на регулируемых опорах; открытая система: без фасадов.
3. Кромка: скрытые торцы 0,4 мм, видимые 2 мм (ПВХ/АБС).
4. Присадка по 32-й системе — выполняет цех.
5. Зазор до потолка 600 мм.
6. Подъём корпуса: диагональ боковины без цоколя √(2120² + 500²) = 2178 мм < 2800 мм до потолка — корпус собирается лёжа, поднимается поворотом и ставится на цоколь.
7. Крепление к стене от опрокидывания — уголки 2 шт. к несущему основанию (монтажная схема шкафов).

3D орто

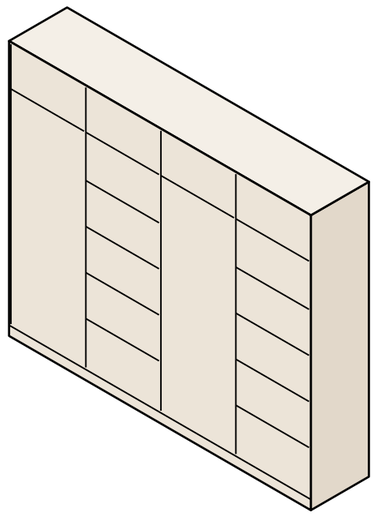


					Проект: Дом 331 м²	М 1:25
	Лист	№ док.	Подпись	Дата	Система хранения М_23	
Дизайнер	Кырлан А.С.			04.11.26		


Стадия	Лист	Листов
П	Д_2	168

выпуск 04.11.2026 № f163a372b2 · стр. 149 из 168


Вид с фасадами

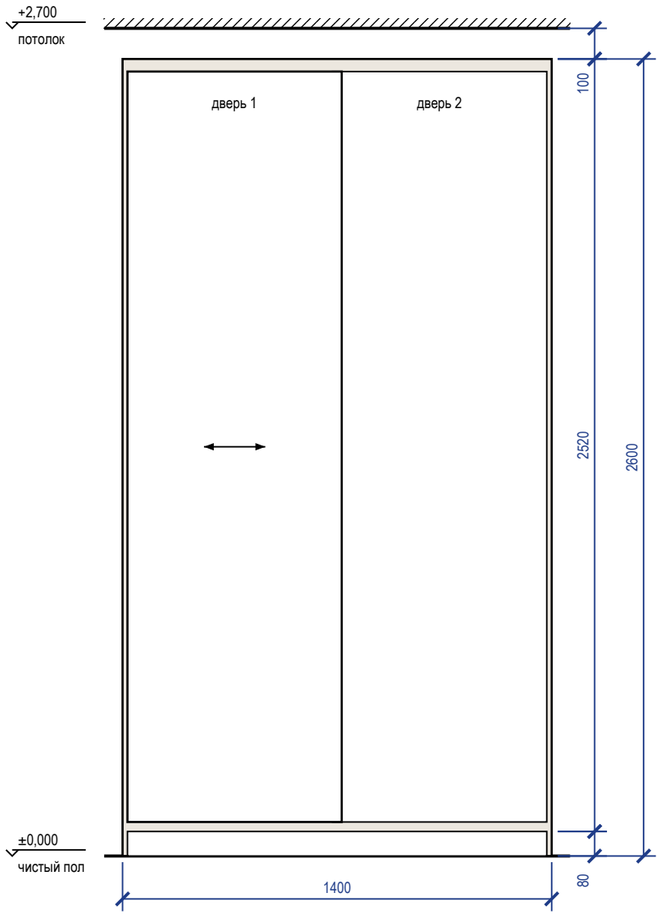


Вид без фасадов

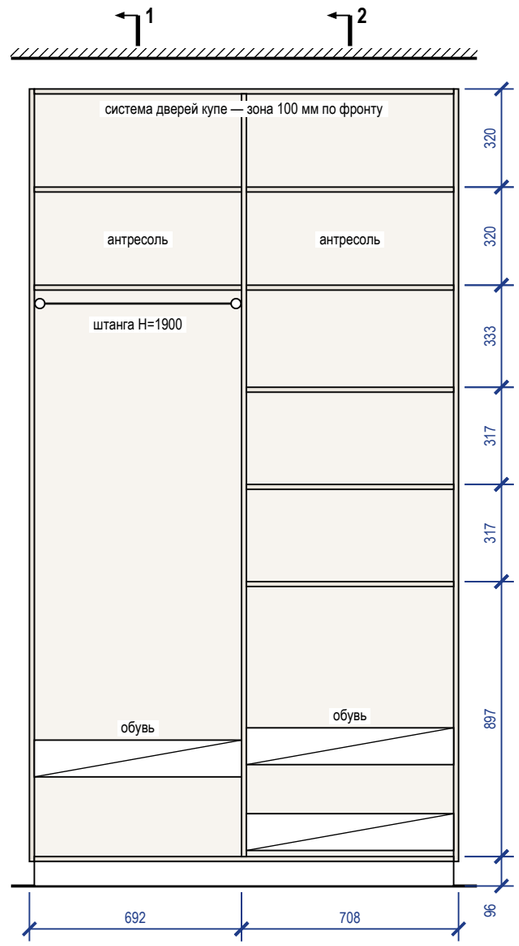

Разрез 1-1

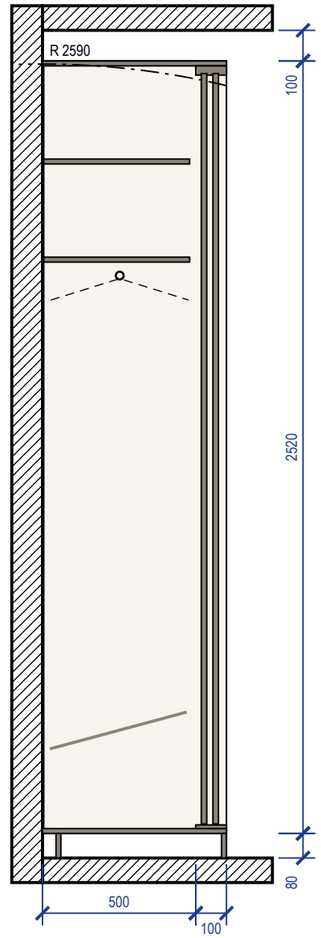


Разрез 2-2

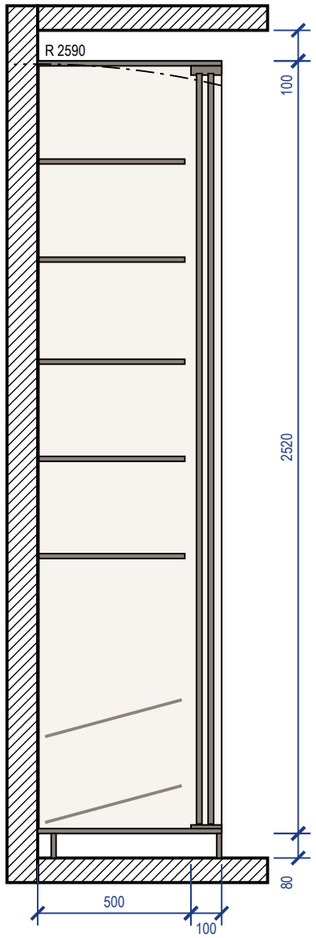

Примечания

1. Размеры — в мм по чистовой отделке; изделие 1400×600×2600 (Ш×Г×В). Перед раскроем — контрольный замер цеха после чистовой отделки стен, пола и потолка.
2. Корпус — ЛДСП 16 мм, задняя стенка ХДФ 4 мм в паз, цоколь 80 мм на регулируемых опорах; двери купе — ЛДСП 10 мм в алюминиевом профиле; нахлёст 30 мм, ширина двери 699 мм, высота — проём минус 40 мм; цвет — по колерной карте.
3. Кромка: скрытые торцы 0,4 мм, видимые 2 мм (ПВХ/АБС).
4. Номинальные зазоры: дверь купе — боковина 3 мм, фасад ящика — стойка 2 мм; ящики внутри купе — с накладкой 30 мм на стойке со стороны нахлёста дверей.
5. Присадка по 32-й системе — выполняет цех.
6. Зазор до потолка 100 мм — закрыть планкой в цвет корпуса при монтаже.
7. Подъём корпуса: диагональ боковины без цоколя $\sqrt{(2520^2 + 600^2)} = 2590$ мм < 2700 мм до потолка — корпус собирается лёжа, поднимается поворотом и ставится на цоколь.
8. Крепление к стене от опрокидывания — уголки 2 шт. к несущему основанию (монтажная схема шкафов).


3D орто

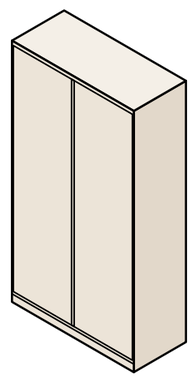


					Проект: Дом 331 м²	**М 1:20**
	Лист	№ док.	Подпись	Дата	Шкаф-купе М_24	Стадия / Лист / Листов
Дизайнер	Кырлан А.С.			04.11.26		П / Д_3 / 168

выпуск 04.11.2026 № f163a372b2 · стр. 150 из 168


Общий вид

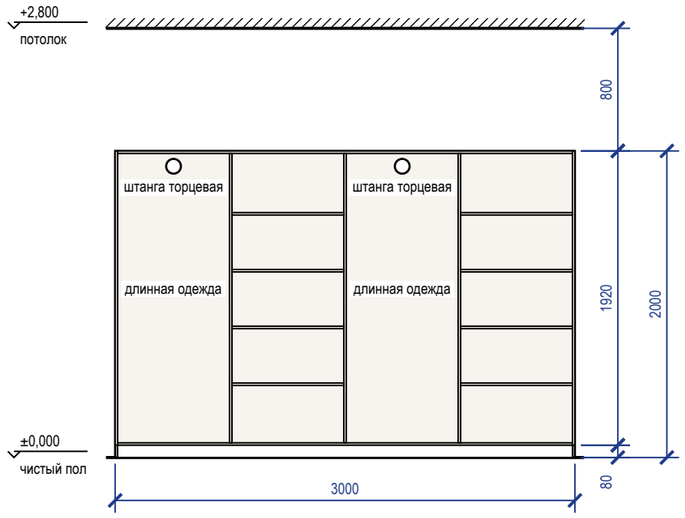


Наполнение, размеры в свету

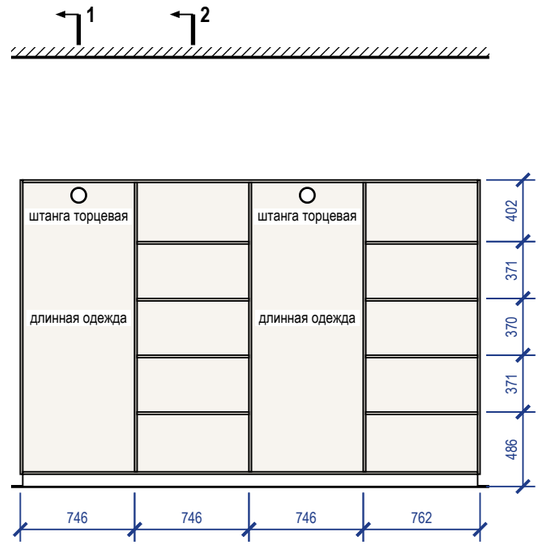

Разрез 1-1

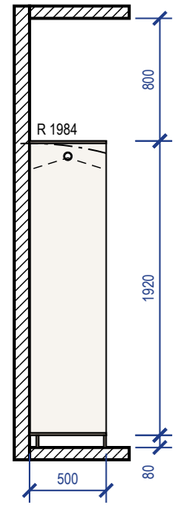


Разрез 2-2

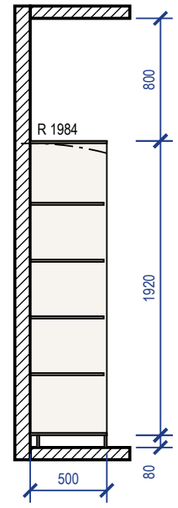

Примечания


1. Размеры — в мм по чистовой отделке; изделие 3000×500×2000 (Ш×Г×В). Перед раскроем — контрольный замер цеха после чистовой отделки стен, пола и потолка.
2. Корпус — ЛДСП 16 мм, задняя стенка ХДФ 4 мм в паз, цоколь 80 мм на регулируемых опорах; открытая система: без фасадов.
3. Кромка: скрытые торцы 0,4 мм, видимые 2 мм (ПВХ/АБС).
4. Присадка по 32-й системе — выполняет цех.
5. Зазор до потолка 800 мм.
6. Подъём корпуса: диагональ боковины без цоколя √(1920² + 500²) = 1984 мм < 2800 мм до потолка — корпус собирается лёжа, поднимается поворотом и ставится на цоколь.
7. Крепление к стене от опрокидывания — уголки 2 шт. к несущему основанию (монтажная схема шкафов).

3D орто

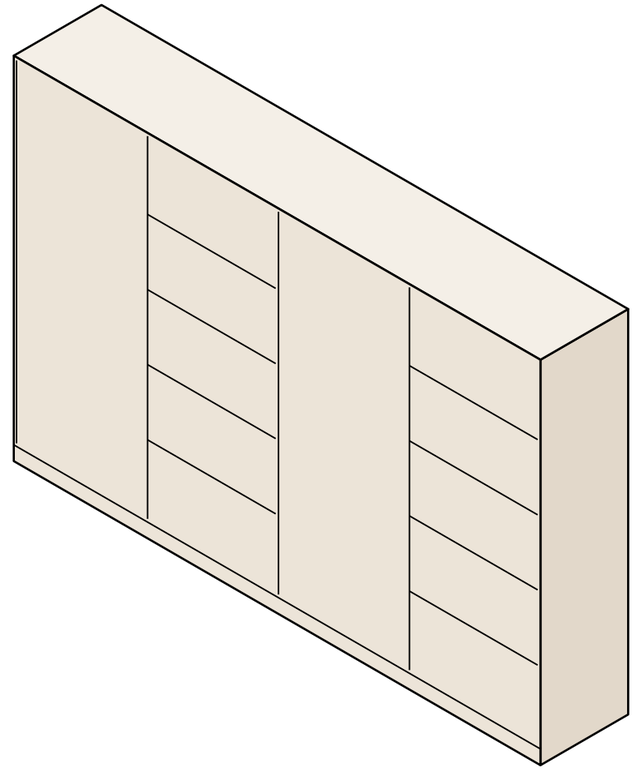


					Проект: Дом 331 м²	**М 1:40**
	Лист	№ док.	Подпись	Дата		
Дизайнер	Кырлан А.С.			04.11.26	Система хранения М_26	Стадия: П; Лист: Д_4; Листов: 168


Общий вид

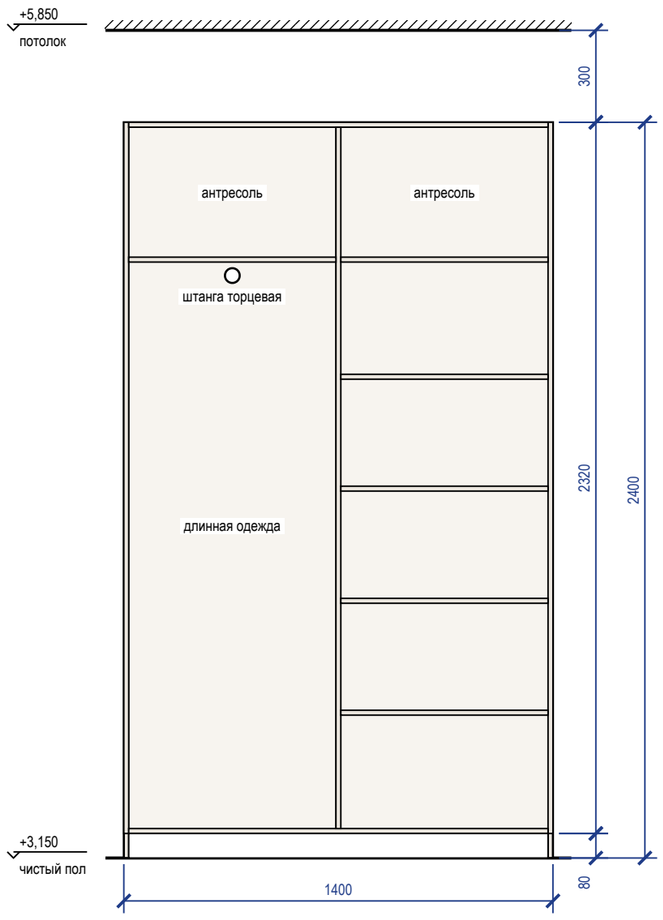


Наполнение, размеры в свету

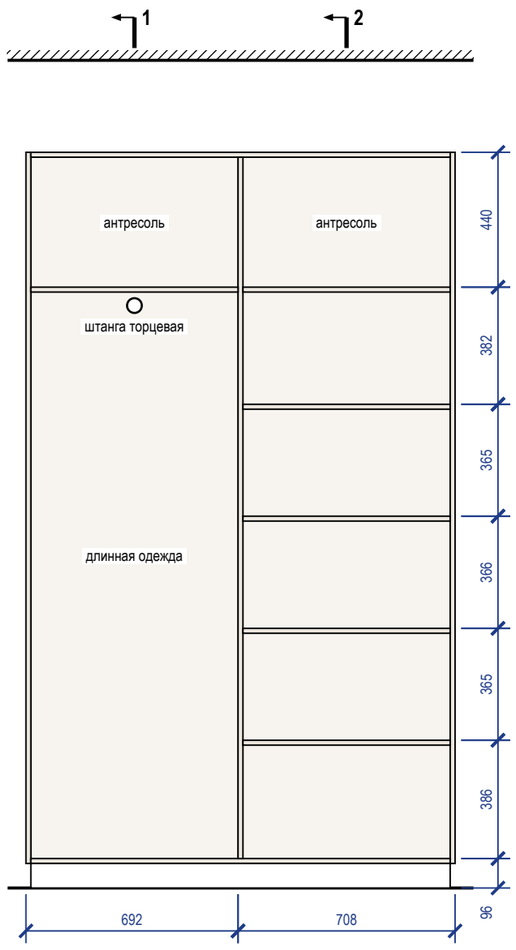

Разрез 1-1

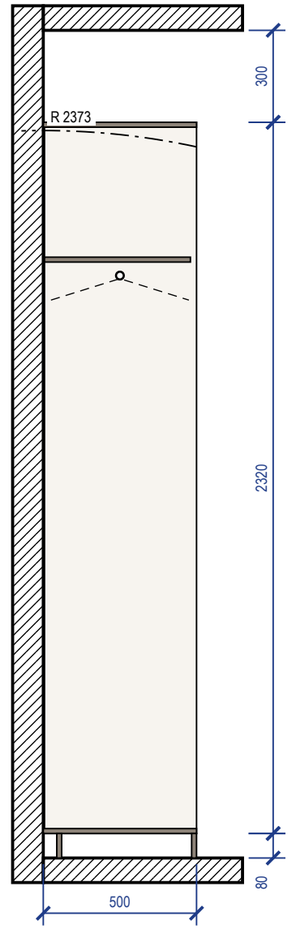


Разрез 2-2

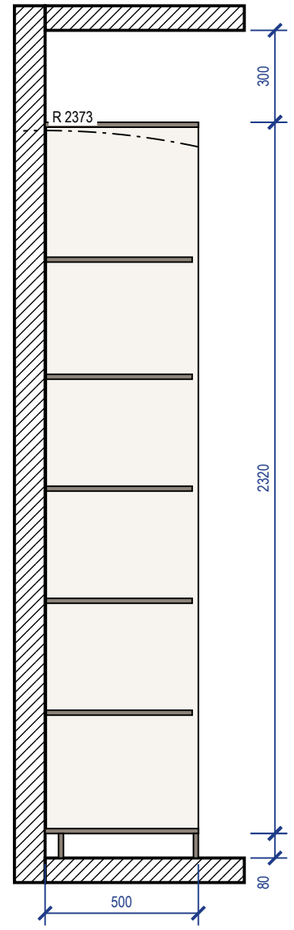

Примечания


1. Размеры — в мм по чистовой отделке; изделие 1400×500×2400 (Ш×Г×В). Перед раскроем — контрольный замер цеха после чистовой отделки стен, пола и потолка.
2. Корпус — ЛДСП 16 мм, задняя стенка ХДФ 4 мм в паз, цоколь 80 мм на регулируемых опорах; открытая система: без фасадов.
3. Кромка: скрытые торцы 0,4 мм, видимые 2 мм (ПВХ/АБС).
4. Присадка по 32-й системе — выполняет цех.
5. Зазор до потолка 300 мм.
6. Подъём корпуса: диагональ боковины без цоколя $\sqrt{(2320^2 + 500^2)} = 2373$ мм < 2700 мм до потолка — корпус собирается лёжа, поднимается поворотом и ставится на цоколь.
7. Крепление к стене от опрокидывания — уголки 2 шт. к несущему основанию (монтажная схема шкафов).

3D орто

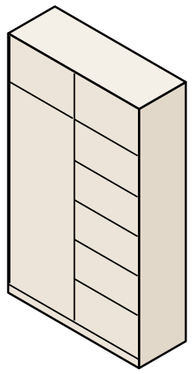


					Проект: Дом 331 м²	М 1:20
	Лист	№ док.	Подпись	Дата		
Дизайнер	Кырлан А.С.			04.11.26	Система хранения М_43	Стадия / Лист / Листов
						П / Д_5 / 168


Вид с фасадами

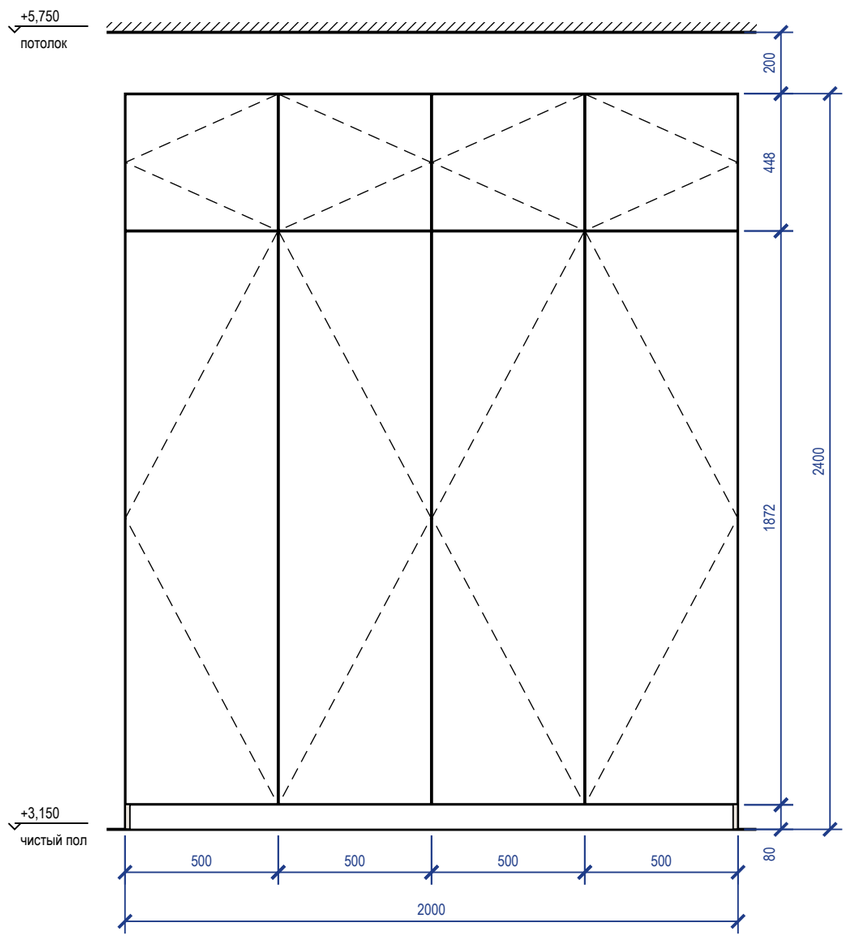


Вид без фасадов

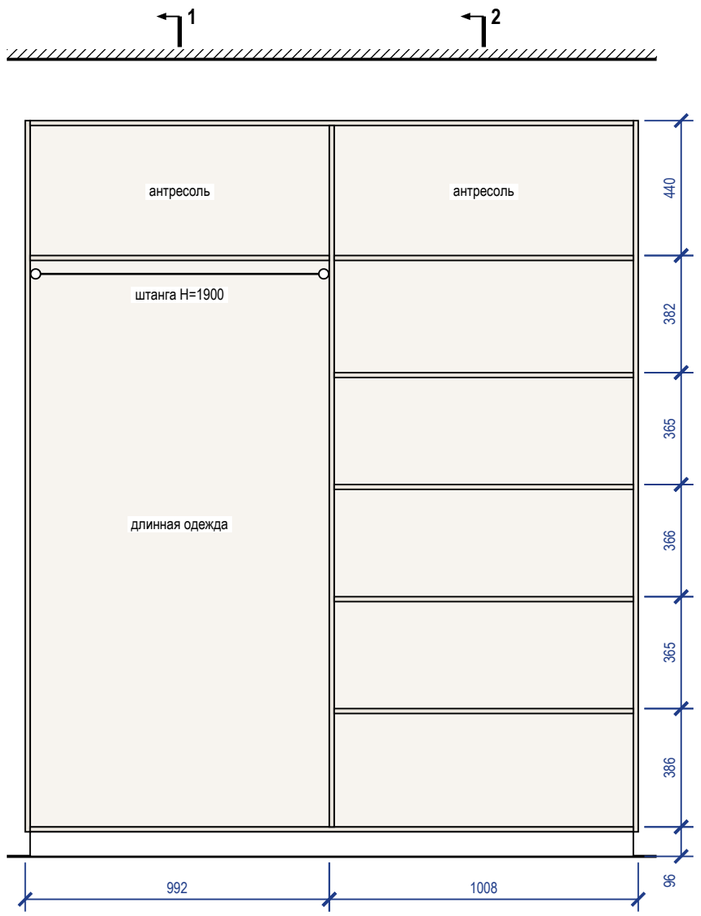

Разрез 1-1

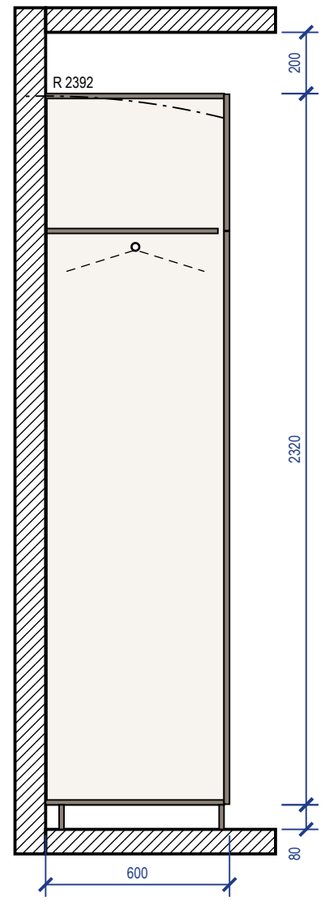


Разрез 2-2

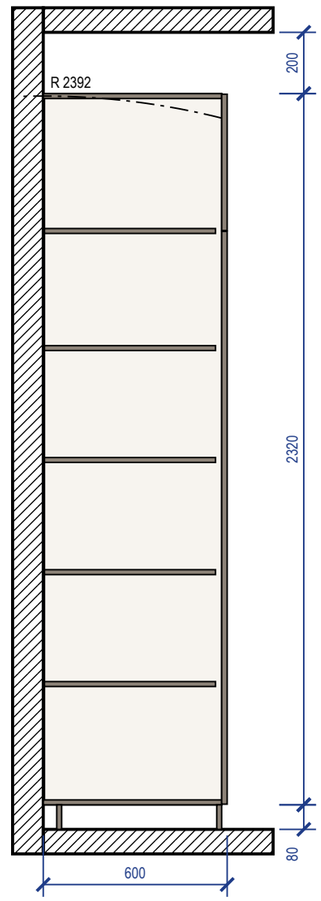

Примечания


1. Размеры — в мм по чистовой отделке; изделие 2000×600×2400 (Ш×Г×В). Перед раскроем — контрольный замер цеха после чистовой отделки стен, пола и потолка.
2. Корпус — ЛДСП 16 мм, задняя стенка ХДФ 4 мм в паз, цоколь 80 мм на регулируемых опорах; фасады накладные — МДФ 18 мм, эмаль матовая, 18 мм; цвет — по колерной карте; петли с доводчиком: фасад 1869 мм — 4 петли, фасад 445 мм — 2 петли.
3. Кромка: скрытые торцы 0,4 мм, видимые 2 мм (ПВХ/АБС).
4. Номинальные зазоры: между фасадами 3 мм, фасад — стена и фасад — потолок не менее 3 мм, фасад ящика — стойка 2 мм.
5. Присадка по 32-й системе — выполняет цех.
6. Зазор до потолка 200 мм.
7. Подъём корпуса: диагональ боковины без цоколя $\sqrt{(2320^2 + 582^2)} = 2392$ мм < 2600 мм до потолка — корпус собирается лёжа, поднимается поворотом и ставится на цоколь.
8. Крепление к стене от опрокидывания — уголки 2 шт. к несущему основанию (монтажная схема шкафов).

3D орто

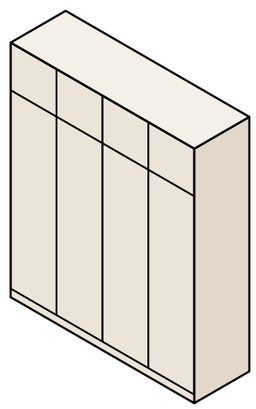


					Проект: Дом 331 м²	М 1:20
	Лист	№ док.	Подпись	Дата		
Дизайнер	Кырлан А.С.			04.11.26	Шкаф распашной М_46	Стадия / Лист / Листов
						П / Д_6 / 168


Общий вид

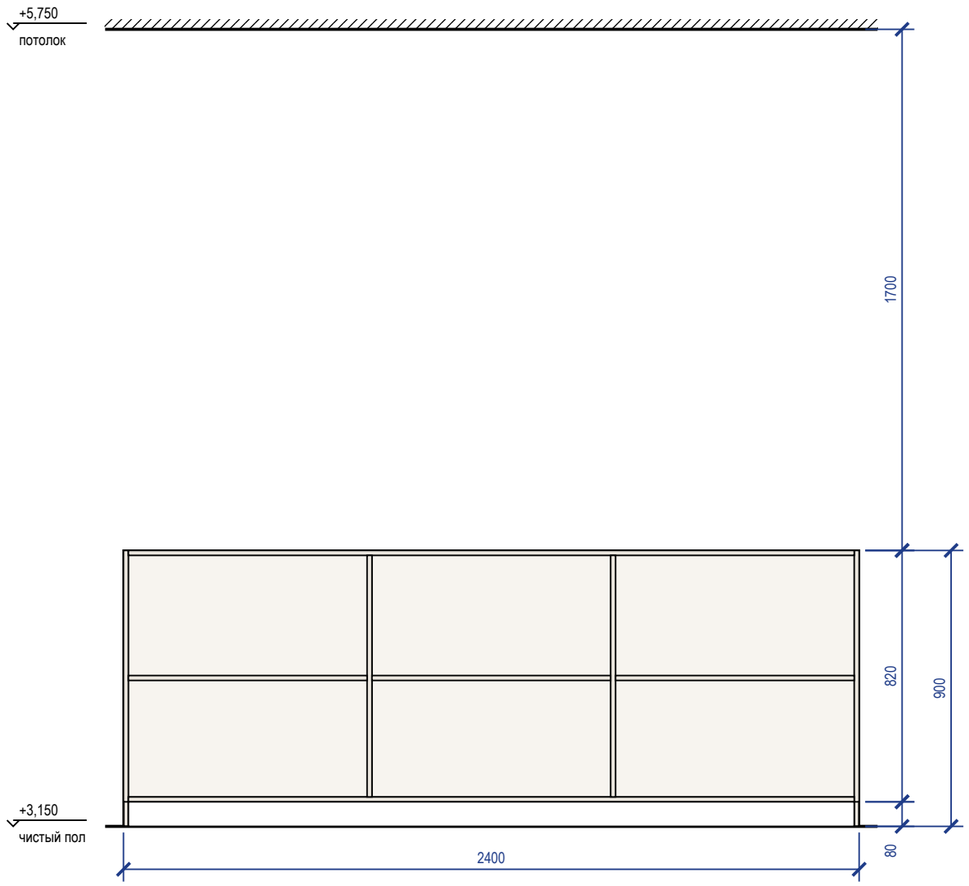

Наполнение, размеры в свету

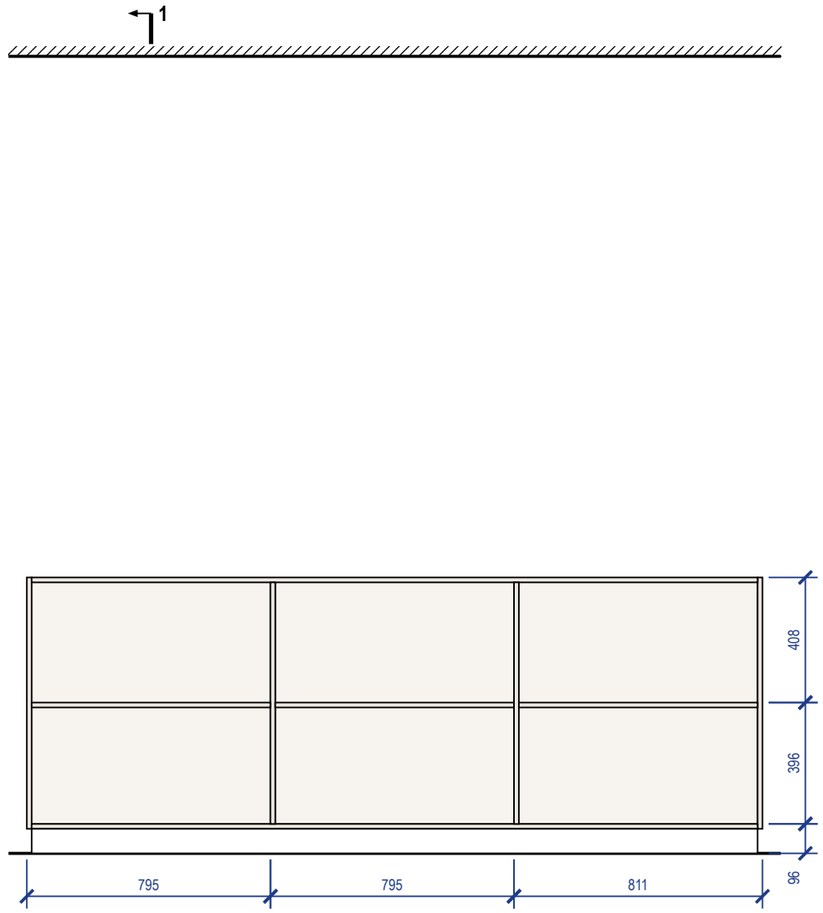


Разрез 1-1

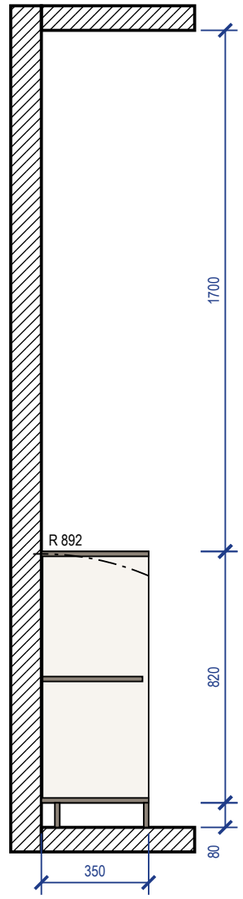

Примечания

1. Размеры — в мм по чистовой отделке; изделие 2400×350×900 (Ш×Г×В). Перед раскроем — контрольный замер цеха после чистовой отделки стен, пола и потолка.
2. Корпус — ЛДСП 16 мм, задняя стенка ХДФ 4 мм в паз, цоколь 80 мм на регулируемых опорах; открытая система: без фасадов.
3. Кромка: скрытые торцы 0,4 мм, видимые 2 мм (ПВХ/АБС).
4. Присадка по 32-й системе — выполняет цех.
5. Зазор до потолка 1700 мм.
6. Подъём корпуса: диагональ боковины без цоколя $\sqrt{(820^2 + 350^2)} = 892$ мм < 2600 мм до потолка — корпус собирается лёжа, поднимается поворотом и ставится на цоколь.
7. Крепление к стене от опрокидывания — уголки 2 шт. к несущему основанию (монтажная схема шкафов).


3D орто

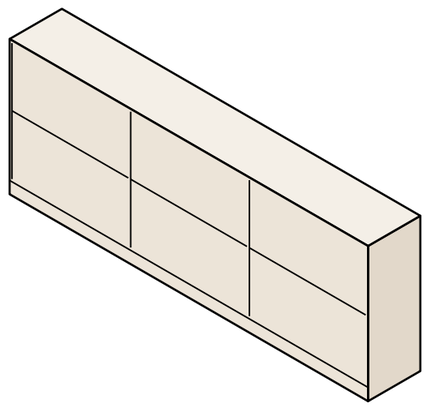


					Проект: Дом 331 м²	**М 1:20**
	Лист	№ док.	Подпись	Дата		
Дизайнер	Кырлан А.С.			04.11.26	Система хранения М_49	
					Стадия: П	Лист: Д_7
					Листов: 168	

выпуск 04.11.2026 № f163a372b2 · стр. 154 из 168


Вид с фасадами

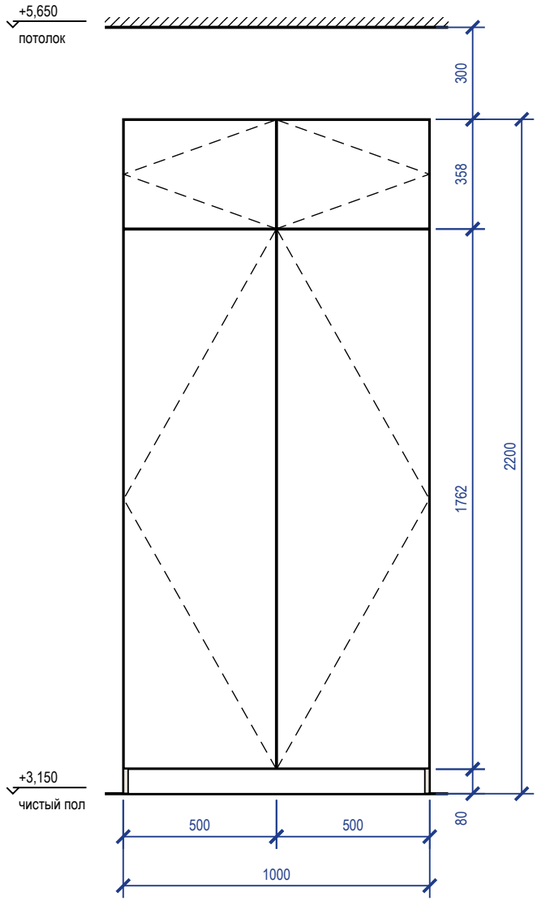

Вид без фасадов

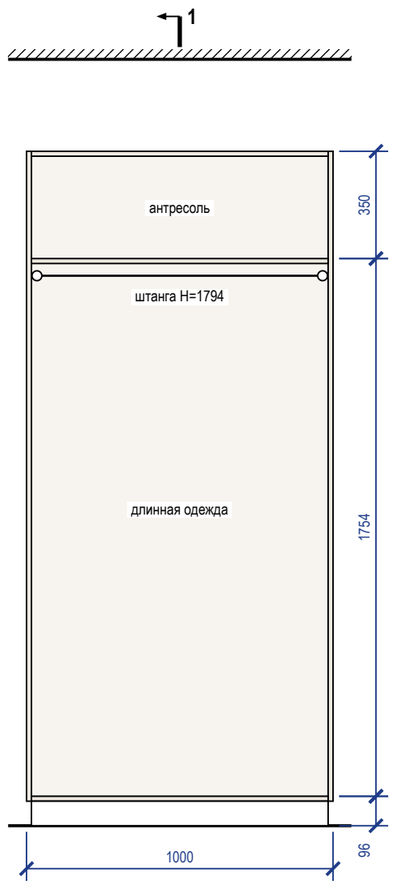


Разрез 1-1

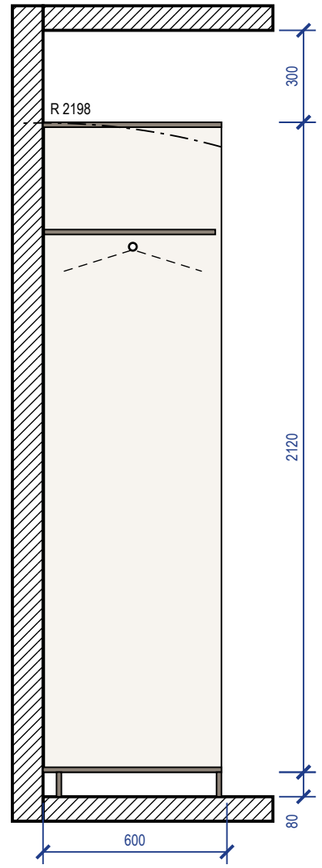

Примечания

1. Размеры — в мм по чистовой отделке; изделие 1000×600×2200 (Ш×Г×В). Перед раскроем — контрольный замер цеха после чистовой отделки стен, пола и потолка.
2. Корпус — ЛДСП 16 мм, задняя стенка ХДФ 4 мм в паз, цоколь 80 мм на регулируемых опорах; фасады накладные — МДФ 18 мм, эмаль матовая, 18 мм; цвет — по колерной карте; петли с доводчиком: фасад 1759 мм — 4 петли, фасад 355 мм — 2 петли.
3. Кромка: скрытые торцы 0,4 мм, видимые 2 мм (ПВХ/АБС).
4. Номинальные зазоры: между фасадами 3 мм, фасад — стена и фасад — потолок не менее 3 мм, фасад ящика — стойка 2 мм.
5. Присадка по 32-й системе — выполняет цех.
6. Зазор до потолка 300 мм.
7. Подъём корпуса: диагональ боковины без цоколя $\sqrt{(2120^2 + 582^2)} = 2198$ мм < 2500 мм до потолка — корпус собирается лёжа, поднимается поворотом и ставится на цоколь.
8. Крепление к стене от опрокидывания — уголки 2 шт. к несущему основанию (монтажная схема шкафов).


3D орто

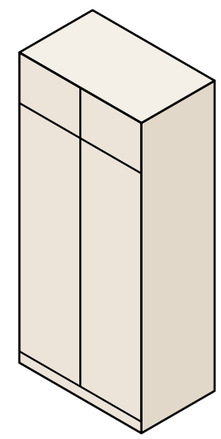


					Проект: Дом 331 м²	М 1:20
	Лист	№ док.	Подпись	Дата		
Дизайнер	Кырлан А.С.			04.11.26	Шкаф распашной М_53	Стадия: П; Лист: Д_8; Листов: 168

выпуск 04.11.2026 № f163a372b2 · стр. 155 из 168


Вид с фасадами

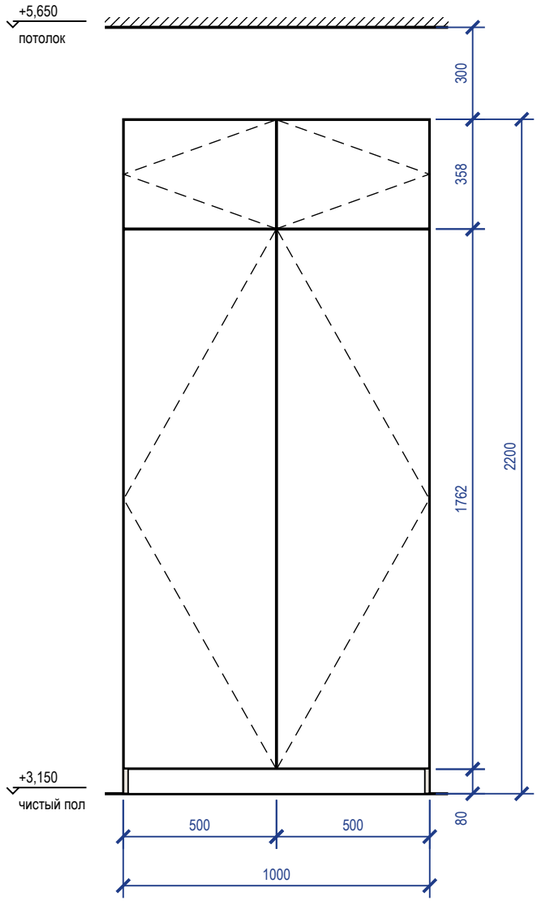

Вид без фасадов

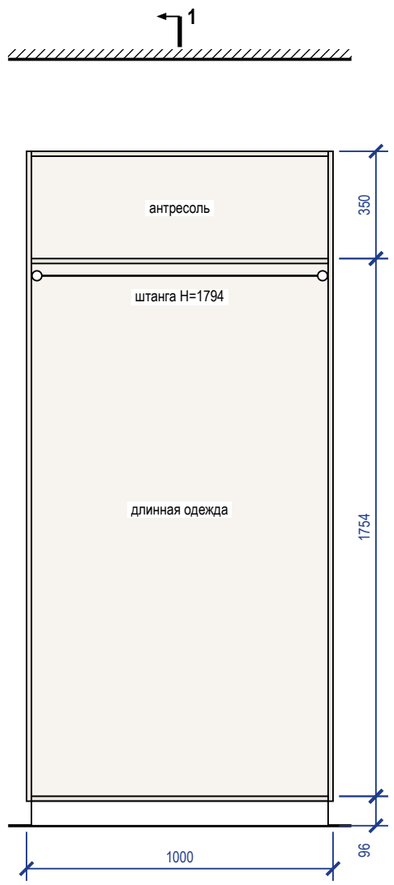


Разрез 1-1

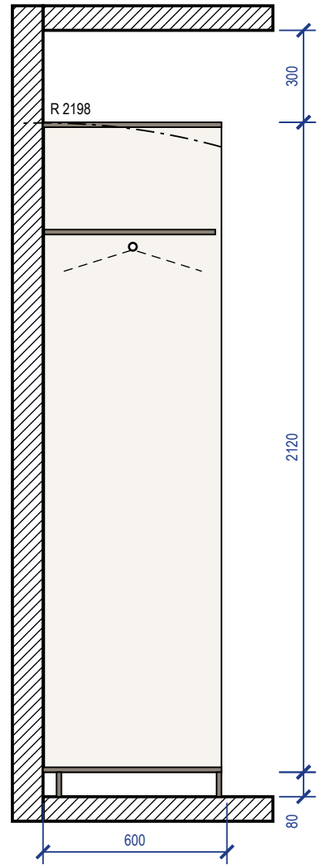

Примечания

1. Размеры — в мм по чистовой отделке; изделие 1000×600×2200 (Ш×Г×В). Перед раскроем — контрольный замер цеха после чистовой отделки стен, пола и потолка.
2. Корпус — ЛДСП 16 мм, задняя стенка ХДФ 4 мм в паз, цоколь 80 мм на регулируемых опорах; фасады накладные — МДФ 18 мм, эмаль матовая, 18 мм; цвет — по колерной карте; петли с доводчиком: фасад 1759 мм — 4 петли, фасад 355 мм — 2 петли.
3. Кромка: скрытые торцы 0,4 мм, видимые 2 мм (ПВХ/АБС).
4. Номинальные зазоры: между фасадами 3 мм, фасад — стена и фасад — потолок не менее 3 мм, фасад ящика — стойка 2 мм.
5. Присадка по 32-й системе — выполняет цех.
6. Зазор до потолка 300 мм.
7. Подъём корпуса: диагональ боковины без цоколя $\sqrt{(2120^2 + 582^2)} = 2198$ мм < 2500 мм до потолка — корпус собирается лёжа, поднимается поворотом и ставится на цоколь.
8. Крепление к стене от опрокидывания — уголки 2 шт. к несущему основанию (монтажная схема шкафов).


3D орто

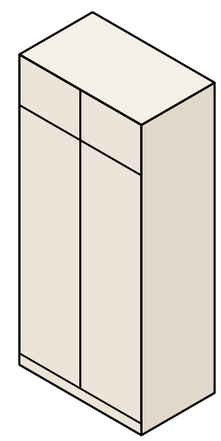


					Проект: Дом 331 м²	**М 1:20**
	Лист	№ док.	Подпись	Дата	Шкаф распашной М_56	Стадия / Лист / Листов
Дизайнер	Кырлан А.С.			04.11.26		П / Д_9 / 168

выпуск 04.11.2026 № f163a372b2 · стр. 156 из 168


Вид с фасадами

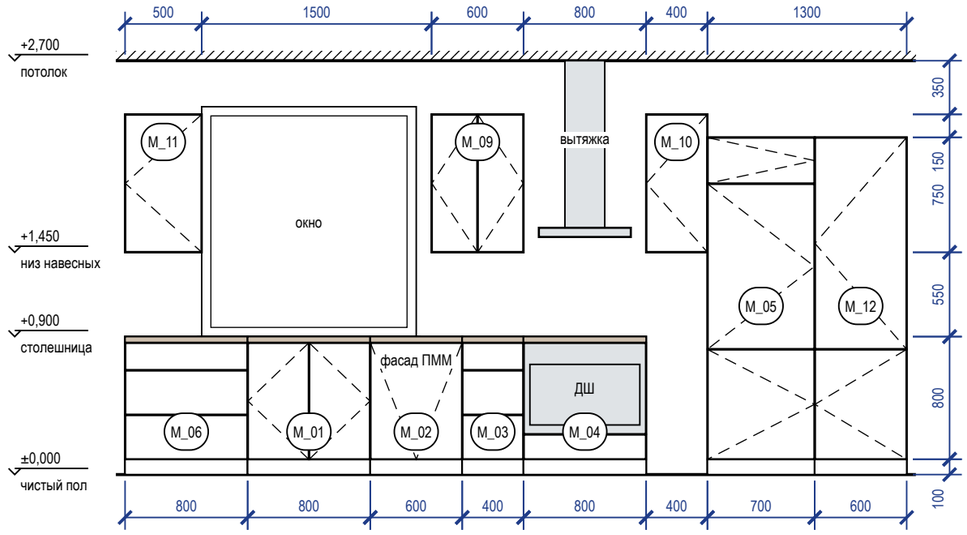


Вид без фасадов (наполнение, выводы)

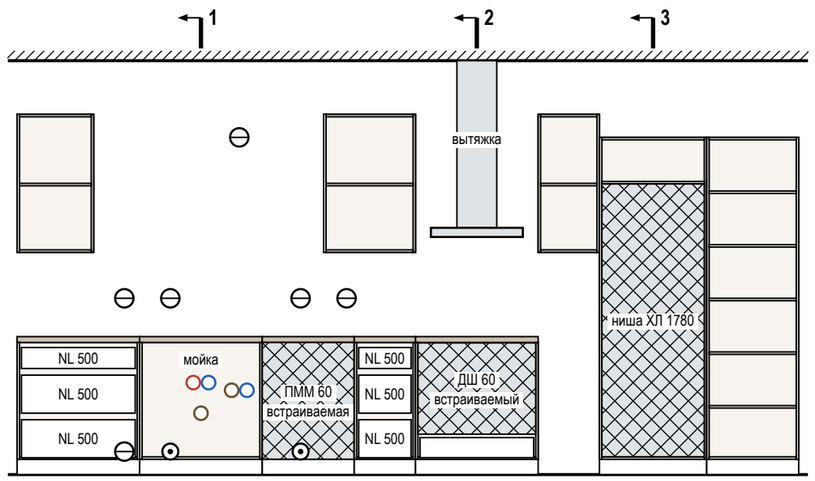


Разрез 1-1

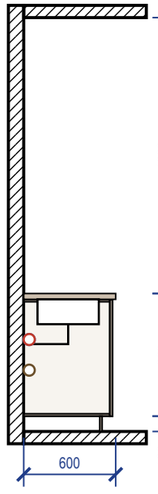


Разрез 2-2

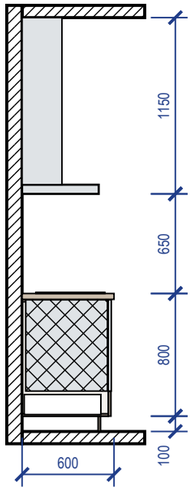

Разрез 3-3

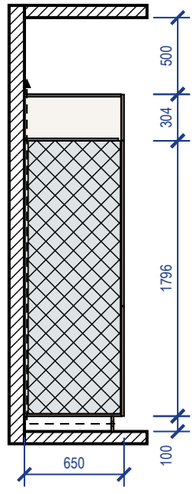

3D орто

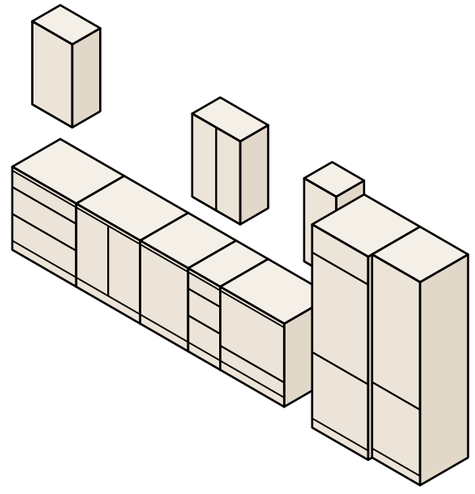


Примечания

1. Размеры — в мм по чистовой отделке, вид из помещения; марки — как на плане расстановки. Перед раскроем — контрольный замер цеха после фартука и пола.
2. Корпуса — ЛДСП 16 мм, задняя стенка ХДФ 4 мм; фасады — МДФ, эмаль матовая 18 мм, цвет по колерной карте; столешница 38 мм, свес 20 мм; цоколь 100 мм.
3. Кромка: скрытые торцы 0,4 мм, видимые 2 мм. Номинальные зазоры: между фасадами 3 мм, фасад — столешница 3 мм, фасад — стена не менее 3 мм.
4. Ящики полного выдвижения и петли — с доводчиком; присадка по 32-й системе — выполняет цех.
5. Низ вытяжки — не ниже 650 мм над варочной панелью или по паспорту модели; короб воздуховода — до потолка.
6. Ниши техники (холодильник — ориентир 1780 мм) — по монтажным схемам выбранных моделей: решётка в цоколе и канал за пеналом холодильника, зазор за духовым шкафом, фасад ПММ на двери машины.

					Проект: Дом 331 м²	**М 1:40**
	Лист	№ док.	Подпись	Дата		
Дизайнер	Кырлан А.С.			04.11.26	Кухня (пом. 1). Развёртка гарнитура	Стадия: П; Лист: Д_10; Листов: 168


выпуск 04.11.2026 № f163a372b2 · стр. 157 из 168

План (вид сверху)

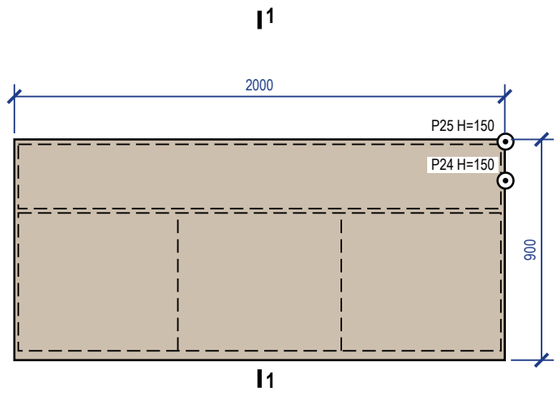


▲ рабочая сторона — северная (к стене А), проход 1100


Вид с рабочей стороны

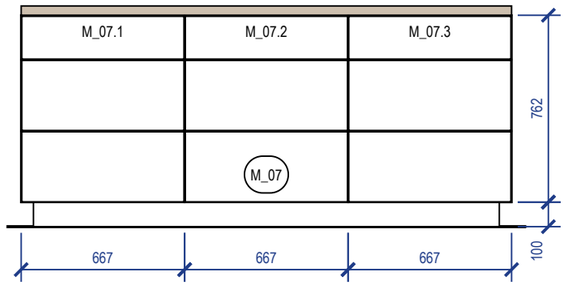


Вид без фасадов (наполнение, вывод)

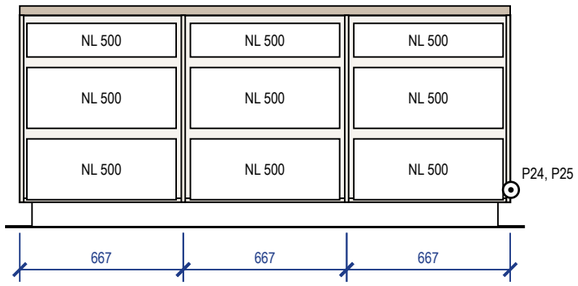

Разрез 1-1

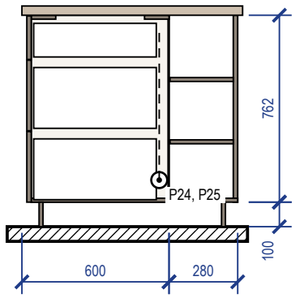

3D орто

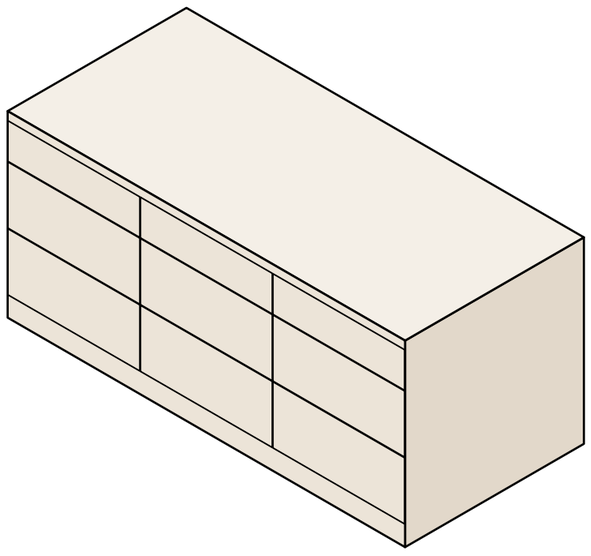

Примечания

1. Размеры — в мм по чистовому полу; перед раскроем — контрольный замер цеха после укладки пола. Остров крепится к полу (уголки в цоколе), выравнивается опорами ±20 мм.
2. Корпуса — ЛДСП 16 мм, задняя стенка ХДФ 4 мм; фасады — МДФ, эмаль матовая 18 мм; столешница 38 мм (материал — по наименованию изделия: столешница кварц), свес 20 мм по периметру; цоколь 100 мм с отступом 50 мм.
3. Кромка: скрытые торцы 0,4 мм, видимые 2 мм. Номинальные зазоры: между фасадами 3 мм, фасад — столешница 3 мм.
4. Рабочая сторона — северная (к стене А): проход 1100 мм; с тыла — открытые полки глубиной 262 мм. Членение и сторона — предложение мебельщика.
5. Питание: P24 — торцевая панель острова M_07: мелкая техника, H=150; P25 — торцевая панель острова M_07: мелкая техника, H=150; кабель — внутри модуля до панели, доступ через съёмный цоколь.

Спецификация изделия M_07

Поз.	Наименование	Тип, размер	Кол.
M_07.1	модуль с ящиками	667×900×900	1
M_07.2	модуль с ящиками	667×900×900	1
M_07.3	модуль с ящиками	667×900×900	1
	Направляющие полного выдвижения с доводчиком NL 500	пара	9
	Ручка-профиль	латунь матовая	9
	Опора кухонная регулируемая 100–120 мм	+ клипса цоколя	18
	Уголок крепления острова к полу	стальной, в цоколе	4
	Полкодержатель с фиксацией	ø5 мм	24

					Проект: Дом 331 м²	**M 1:25**
	Лист	№ док.	Подпись	Дата		
Дизайнер	Кырлан А.С.			04.11.26	Остров M_07 (пом. 1). Чертёж изделия	Стадия: П; Лист: Д_11; Листов: 168

Ведомость отделки помещений (форма 1 прил. А ГОСТ 21.501-2018). Лист 1 из 4

№	Наименование помещения	Потолок			Стены и перегородки			Низ стен (плинтус)			Пол		Примечание
		Вид отделки	Код цвета	S, м²	Вид отделки	Код цвета	S, м²	Вид отделки	Код цвета	L, м	Вид отделки	S, м²	
1	Кухня-столовая 24,59 м²	ГКЛ по каркасу П113, отм. +2,700; +2,550; +2,600; окраска, Tikkurila Luja 7, матовая, 2 слоя, подготовка Q3	NCS S 0804-Y30R	24,59	Окраска, Tikkurila Luja 7, полуматовая, 2 слоя, подготовка К3 Фартук кухни (стена А): облицовка керамогранитом, аналог: керамогранит матовый, тон F497, 600×600×9 мм, клей C2 TE S1, затирка CG2WA	NCS S 0804-Y30R #F1F1EC	44,80 1,15	Плинтус МДФ h=80 мм, аналог: МДФ под окраску 80×16 мм	NCS S 0804-Y30R	18,3	Инженерная доска, 1167-4250, 2100×127 мм, на клею; тип 1, отм. ЧП ±0,000	24,59	Н стен 2700 (до потолка); влагостойкая полуматовая окраска (класс мокрого истирания 1 по EN 13300); категория К3 по СП 71.13330.2017, табл. 7.5; по ГКЛ каркаса П113, влагостойкая окраска; Q3 колеруется в код стен, но по эмали на МДФ: сличать отдельным выкрасом на своей подложке (выкрас № 10); плинтус в цвет: стены
2	Кабинет-гостевая 11,92 м²	ГКЛ по каркасу П113, отм. +2,700; +2,600; окраска, Little Greene Absolute Matt, глубокоматовая, 2 слоя, подготовка Q3	Little Greene No. 105	11,92	Окраска, Farrow & Ball Modern Emulsion, матовая, 2 слоя, подготовка Q3 Акцент — стена А: окраска, Farrow & Ball Modern Emulsion, матовая, 2 слоя, подготовка Q3	Farrow & Ball No. 226 Farrow & Ball No. 298	25,30 5,68	Плинтус МДФ h=80 мм, аналог: МДФ под покраску 80×16	Farrow & Ball No. 226	11,7	Инженерная доска, 1167-4250, 2100×127 мм, на клею; тип 2, отм. ЧП ±0,000	11,92	Н стен 2700 (до потолка); краска бренда веера Little Greene; класс по EN 13300 и блеск линейки — по ТУ Little Greene, в базе не сверены; плинтус в цвет: стены
3	Санузел 1 этажа 4,87 м²	ГКЛВ по каркасу П113, отм. +2,600; окраска, Little Greene Intelligent Bathroom, матовая, 2 слоя, подготовка Q3	Little Greene No. 105	4,87	Облицовка плиткой, A8UZ, 600×1200×9 мм, клей C2 TE S1, затирка CG2WA	Atlas Concorde A8UZ	20,53	нет			Аналог: керамогранит ректифицированный под травертин, матовый, 600×600×9 мм; тип 3, отм. ЧП −0,015	4,87	Н стен 2615 (до потолка); гидроизоляция обмазочная, 2 слоя, по всему помещению, с заведением на стены 200 мм; у душа — на всю высоту стен душевой зоны и 500 мм за край душевой зоны (по пирогу пола); тест проливом и акт скрытых работ; краска бренда веера Little Greene класс по EN 13300 и блеск линейки — по ТУ Little Greene, в базе не сверены
4	Котельная 6,88 м²	Потолок под покраску, отм. +2,800; окраска, Little Greene Absolute Matt, глубокоматовая, 2 слоя, подготовка Q3	Little Greene No. 105	6,88	Окраска, Farrow & Ball Modern Emulsion, матовая, 2 слоя, подготовка Q3	Farrow & Ball No. 226	26,96	Плинтус МДФ h=80 мм, аналог: МДФ под покраску 80×16	Farrow & Ball No. 226	9,7	Керамогранит, A8UZ, 600×1200×9 мм; тип 4, отм. ЧП ±0,000	6,88	Н стен 2800 (до потолка); матовая моющаяся, класс 1 EN 13300 — осознанно вместо полуматовой; краска бренда веера Little Greene класс по EN 13300 и блеск линейки — по ТУ Little Greene, в базе не сверены; плинтус в цвет: стены
5	Гостиная 33,74 м²	ГКЛ по каркасу П113, отм. +2,600; +2,700; окраска, Tikkurila Anti-Reflex 2, глубокоматовая, 2 слоя, подготовка Q3	NCS S 0804-Y30R	33,74	Окраска, Tikkurila Optiva 5 Matt, матовая, 2 слоя, подготовка К3 Акцент — стена А: окраска, Farrow & Ball Modern Emulsion, матовая, 3 слоя, аналог: интерьерная краска, класс 2 по EN 13300, глубокоматовая/матовая, база С, подготовка К3	NCS S 0804-Y30R Farrow & Ball No. 93	32,20 12,92	Плинтус МДФ h=80 мм, аналог: МДФ под окраску 80×16 мм	NCS S 0804-Y30R	18,2	Инженерная доска, 1167-4250, 2100×127 мм, на клею; тип 5, отм. ЧП ±0,000	33,74	Н стен 2600 (до потолка); колеруется в код стен, но по эмали на МДФ: сличать отдельным выкрасом на своей подложке (выкрас № 10); плинтус в цвет: стены

Примечания

1. Ведомость продолжена на листе 2 из 4; итоги, сводка площадей и примечания — на последнем листе ведомости.

					Проект: Дом 331 м²
	Лист	№ док.	Подпись	Дата	Ведомость отделки помещений. Лист 1 из 4
Дизайнер	Кырлан А.С.			04.11.26	

Стадия	Лист	Листов
П	С1	168

Ведомость отделки помещений (форма 1 прил. А ГОСТ 21.501-2018). Лист 2 из 4

№	Наименование помещения	Потолок			Стены и перегородки			Низ стен (плинтус)			Пол		Примечание
		Вид отделки	Код цвета	S, м²	Вид отделки	Код цвета	S, м²	Вид отделки	Код цвета	L, м	Вид отделки	S, м²	
6	Холл с лестницей 10,02 м²	ГКЛ по каркасу П113, отм. +2,700; окраска, Little Greene Absolute Matt, глубокоматовая, 2 слоя, подготовка Q3	Little Greene No. 105	10,02	Окраска, Farrow & Ball Modern Emulsion, матовая, 2 слоя, подготовка Q3	Farrow & Ball No. 226	22,29	Плинтус МДФ h=80 мм, аналог: МДФ под покраску 80×16	Farrow & Ball No. 226	7,0	Инженерная доска, 1167-4250, 2100×127 мм, на клею; тип 2, отм. ЧП ±0,000	10,02	Н стен 2700 (до потолка); матовая моющаяся, класс 1 EN 13300 — осознанно вместо полуматовой; краска бренда веера Little Greene класс по EN 13300 и блеск линейки — по ТУ Little Greene, в базе не сверены; плинтус в цвет: стены
7	Кладовая 5,99 м²	Потолок под покраску, отм. +2,800; окраска, Little Greene Absolute Matt, глубокоматовая, 2 слоя, подготовка Q3	Little Greene No. 105	5,99	Окраска, Little Greene Intelligent Matt, матовая, 2 слоя, подготовка Q3	Little Greene No. 105	23,28	Плинтус МДФ h=80 мм, аналог: МДФ под покраску 80×16	Little Greene No. 105	7,8	Инженерная доска, 1167-4250, 2100×127 мм, на клею; тип 2, отм. ЧП ±0,000	5,99	Н стен 2800 (до потолка); краска бренда веера Little Greene; класс по EN 13300 и блеск линейки — по ТУ Little Greene, в базе не сверены; краска бренда веера Little Greene класс по EN 13300 и блеск линейки — по ТУ Little Greene, в базе не сверены; плинтус в цвет: стены
8	Прихожая 12,46 м²	ГКЛ по каркасу П113, отм. +2,700; окраска, Little Greene Absolute Matt, глубокоматовая, 2 слоя, подготовка Q3	Little Greene No. 105	12,46	Окраска, Farrow & Ball Modern Emulsion, матовая, 2 слоя, подготовка Q3	Farrow & Ball No. 226	38,99	Плинтус МДФ h=80 мм, аналог: МДФ под покраску 80×16	Farrow & Ball No. 226	13,6	Керамогранит, A8UZ, 600×1200×9 мм; тип 4, отм. ЧП ±0,000	12,46	Н стен 2700 (до потолка); матовая моющаяся, класс 1 EN 13300 — осознанно вместо полуматовой; краска бренда веера Little Greene класс по EN 13300 и блеск линейки — по ТУ Little Greene, в базе не сверены; плинтус в цвет: стены
9	Тамбур 3,49 м²	Потолок под покраску, отм. +2,800; окраска, Little Greene Absolute Matt, глубокоматовая, 2 слоя, подготовка Q3	Little Greene No. 105	3,49	Окраска, Farrow & Ball Modern Emulsion, матовая, 2 слоя, подготовка Q3	Farrow & Ball No. 226	17,07	Плинтус МДФ h=80 мм, аналог: МДФ под покраску 80×16	Farrow & Ball No. 226	5,6	Керамогранит, A8UZ, 600×1200×9 мм; тип 4, отм. ЧП ±0,000	3,49	Н стен 2800 (до потолка); матовая моющаяся, класс 1 EN 13300 — осознанно вместо полуматовой; краска бренда веера Little Greene класс по EN 13300 и блеск линейки — по ТУ Little Greene, в базе не сверены; плинтус в цвет: стены
10	Гараж 41,58 м²	Потолок под покраску, отм. +2,800; окраска, Little Greene Absolute Matt, глубокоматовая, 2 слоя, подготовка Q3	Little Greene No. 105	41,58	Окраска, Farrow & Ball Modern Emulsion, матовая, 2 слоя, подготовка Q3	Farrow & Ball No. 226	62,59	Плинтус ПВХ h=100 мм, аналог: ПВХ влагостойкий 100 мм, серый		22,0	Аналог: наливной полимерный пол (эпоксидный), с кварцевой посыпкой, 3 мм; тип 6, отм. ЧП ±0,000	41,58	Н стен 2800 (до потолка); матовая моющаяся, класс 1 EN 13300 — осознанно вместо полуматовой; краска бренда веера Little Greene класс по EN 13300 и блеск линейки — по ТУ Little Greene, в базе не сверены
11	Веранда 21,84 м²	Потолок под покраску (летнее помещение), отм. +2,800; окраска, Tikkurila Luja 7, матовая, 2 слоя, подготовка Q3	NCS S 0804-Y30R	21,84	Окраска, Tikkurila Luja 7, полуматовая, 2 слоя, подготовка К3	NCS S 0804-Y30R	49,63	Плинтус из керамогранита h=80 мм, аналог: из керамогранита пола, подрезка 80 мм, верхняя кромка с запилом 45°	#B8AFA5	20,5	Керамогранит, A8UZ, 600×1200×10 мм; тип 7, отм. ЧП −0,030	21,84	Н стен 2830 (до потолка); влагостойкая окраска по утеплённой стене; категория К3 по СП 71.13330.2017, табл. 7.5; по ГКЛВ каркаса П113, влагостойкая окраска; Q3

Примечания

1. Ведомость продолжена на листе 3 из 4; итоги, сводка площадей и примечания — на последнем листе ведомости.

					Проект: Дом 331 м²
	Лист	№ док.	Подпись	Дата	Ведомость отделки помещений. Лист 2 из 4
Дизайнер	Кырлан А.С.			04.11.26	

Стадия	Лист	Листов
П	С2	168

Ведомость отделки помещений (форма 1 прил. А ГОСТ 21.501-2018). Лист 3 из 4

№	Наименование помещения	Потолок			Стены и перегородки			Низ стен (плинтус)			Пол		Примечание
		Вид отделки	Код цвета	S, м²	Вид отделки	Код цвета	S, м²	Вид отделки	Код цвета	L, м	Вид отделки	S, м²	
12	Крыльцо 3,38 м²	Потолок под покраску (летнее помещение), отм. +2,800; окраска, Tikkurila Luja 7, матовая, 2 слоя, подготовка Q3	NCS S 0804-Y30R	3,38	Окраска, Tikkurila Luja 7, полуматовая, 2 слоя, подготовка К3	NCS S 0804-Y30R	18,73	Плинтус из керамогранита h=80 мм, аналог: из керамогранита пола, подрезка 80 мм, верхняя кромка с запилом 45°	#B8AFA5	6,4	Керамогранит, A8UZ, 600×1200×10 мм; тип 7, отм. ЧП −0,030	3,38	Н стен 2830 (до потолка); влагостойкая окраска по утеплённой стене; категория К3 по СП 71.13330.2017, табл. 7.5; по ГКЛВ каркаса П113, влагостойкая окраска; Q3
13	Спальня мастер 24,59 м²	ГКЛ по каркасу П113, отм. +5,650; +5,750; окраска, Little Greene Absolute Matt, глубокоматовая, 2 слоя, подготовка Q3	Little Greene No. 105	27,05	Окраска, Farrow & Ball Modern Emulsion, матовая, 2 слоя, подготовка Q3 Акцент — стена А: окраска, Tikkurila Optiva 5 Matt, матовая, 2 слоя, подготовка Q3	Farrow & Ball No. 226 NCS S 7020-G10Y	28,61 7,60	Плинтус МДФ h=80 мм, аналог: МДФ под покраску 80×16	Farrow & Ball No. 226	18,7	Инженерная доска, 1167-4250, 2100×127 мм, на клею; тип 2, отм. ЧП +3,150	24,59	Н стен 2500 (до потолка); краска бренда веера Little Greene; класс по EN 13300 и блеск линейки — по ТУ Little Greene, в базе не сверены; плинтус в цвет: стены
14	Гардеробная мастер 6,74 м²	Обшивка скатов и горизонтальной части мансарды (конструкция — по проекту КР), отм. +5,850; окраска, Little Greene Absolute Matt, глубокоматовая, 2 слоя, подготовка Q3	Little Greene No. 105	8,56	Окраска, Little Greene Intelligent Matt, матовая, 2 слоя, подготовка Q3	Little Greene No. 105	18,68	Плинтус МДФ h=80 мм, аналог: МДФ под покраску 80×16	Little Greene No. 105	9,0	Инженерная доска, 1167-4250, 2100×127 мм, на клею; тип 2, отм. ЧП +3,150	6,74	Н стен 2700 (до потолка); краска бренда веера Little Greene; класс по EN 13300 и блеск линейки — по ТУ Little Greene, в базе не сверены; краска бренда веера Little Greene класс по EN 13300 и блеск линейки — по ТУ Little Greene, в базе не сверены; плинтус в цвет: стены
15	Санузел мастер 6,88 м²	ГКЛВ по каркасу П113, отм. +5,750; окраска, Little Greene Intelligent Bathroom, матовая, 2 слоя, подготовка Q3	Little Greene No. 105	7,84	Облицовка плиткой, A8UZ, 600×1200×9 мм, клей C2 TE S1, затирка CG2WA	Atlas Concorde A8UZ	19,94	нет			Аналог: керамогранит ректифицированный под травертин, матовый, 600×600×9 мм; тип 3, отм. ЧП +3,135	6,88	Н стен 2615 (до потолка); гидроизоляция обмазочная, 2 слоя, с заведением на стены 200 мм; над ванной — до 2000 и 300 мм за борт (по пирогу пола); тест проливом и акт скрытых работ; краска бренда веера Little Greene класс по EN 13300 и блеск линейки — по ТУ Little Greene, в базе не сверены
16	Спальня 2 15,52 м²	ГКЛ по каркасу П113, отм. +5,750; +5,650; окраска, Little Greene Absolute Matt, глубокоматовая, 2 слоя, подготовка Q3	Little Greene No. 105	15,52	Окраска, Farrow & Ball Modern Emulsion, матовая, 2 слоя, подготовка Q3 Акцент — стена А: окраска, Farrow & Ball Modern Emulsion, матовая, 2 слоя, подготовка Q3	Farrow & Ball No. 226 Farrow & Ball No. 64	28,08 7,35	Плинтус МДФ h=80 мм, аналог: МДФ под покраску 80×16	Farrow & Ball No. 226	14,7	Инженерная доска, 1167-4250, 2100×127 мм, на клею; тип 2, отм. ЧП +3,150	15,52	Н стен 2500 (до потолка); краска бренда веера Little Greene; класс по EN 13300 и блеск линейки — по ТУ Little Greene, в базе не сверены; плинтус в цвет: стены
17	Холл мансарды 21,72 м²	ГКЛ по каркасу П113, отм. +5,750; окраска, Little Greene Absolute Matt, глубокоматовая, 2 слоя, подготовка Q3	Little Greene No. 105	23,52	Окраска, Farrow & Ball Modern Emulsion, матовая, 2 слоя, подготовка Q3	Farrow & Ball No. 226	34,75	Плинтус МДФ h=80 мм, аналог: МДФ под покраску 80×16	Farrow & Ball No. 226	14,4	Инженерная доска, 1167-4250, 2100×127 мм, на клею; тип 2, отм. ЧП +3,150	21,72	Н стен 2600 (до потолка); матовая моющаяся, класс 1 EN 13300 — осознанно вместо полуматовой; краска бренда веера Little Greene класс по EN 13300 и блеск линейки — по ТУ Little Greene, в базе не сверены; плинтус в цвет: стены

Примечания

1. Ведомость продолжена на листе 4 из 4; итоги, сводка площадей и примечания — на последнем листе ведомости.

					Проект: Дом 331 м²
	Лист	№ док.	Подпись	Дата	Ведомость отделки помещений. Лист 3 из 4
Дизайнер	Кырлан А.С.			04.11.26	

Стадия	Лист	Листов
П	С3	168

Ведомость отделки помещений (форма 1 прил. А ГОСТ 21.501-2018). Лист 4 из 4

№	Наименование помещения	Потолок			Стены и перегородки			Низ стен (плинтус)			Пол		Примечание
		Вид отделки	Код цвета	S, м²	Вид отделки	Код цвета	S, м²	Вид отделки	Код цвета	L, м	Вид отделки	S, м²	
18	Спальня 3 17,11 м²	ГКЛ по каркасу П113, отм. +5,650; +5,750; окраска, Little Greene Absolute Matt, глубокоматовая, 2 слоя, подготовка Q3	Little Greene No. 105	17,11	Окраска, Farrow & Ball Modern Emulsion, матовая, 2 слоя, подготовка Q3 Акцент — стена А: окраска, Tikkurila Optiva 5 Matt, матовая, 2 слоя, подготовка Q3	Farrow & Ball No. 226 NCS S 3020-G30Y	25,47 12,33	Плинтус МДФ h=69 мм, SX165	Farrow & Ball No. 226	15,6	Инженерная доска, 1167-4250, 2100×127 мм, на клею; тип 2, отм. ЧП +3,150	17,11	Н стен 2500 (до потолка); краска бренда веера Little Greene; класс по EN 13300 и блеск линейки — по ТУ Little Greene, в базе не сверены; плинтус в цвет: стены
19	Спальня 4 16,28 м²	ГКЛ по каркасу П113, отм. +5,650; +5,750; окраска, Little Greene Absolute Matt, глубокоматовая, 2 слоя, подготовка Q3	Little Greene No. 105	18,76	Окраска, Farrow & Ball Modern Emulsion, матовая, 2 слоя, подготовка Q3 Акцент — стена А: окраска, Tikkurila Optiva 5 Matt, матовая, 2 слоя, подготовка Q3	Farrow & Ball No. 226 NCS S 3040-Y70R	15,83 14,85	Плинтус МДФ h=69 мм, SX165	Farrow & Ball No. 226	16,6	Инженерная доска, 1167-4250, 2100×127 мм, на клею; тип 2, отм. ЧП +3,150	16,28	Н стен 2500 (до потолка); краска бренда веера Little Greene; класс по EN 13300 и блеск линейки — по ТУ Little Greene, в базе не сверены; плинтус в цвет: стены
20	Санузел 2 6,29 м²	ГКЛВ по каркасу П113, отм. +5,750; окраска, Little Greene Intelligent Bathroom, матовая, 2 слоя, подготовка Q3	Little Greene No. 105	8,15	Облицовка плиткой, A8UZ, 600×1200×9 мм, клей C2 TE S1, затирка CG2WA	Atlas Concorde A8UZ	17,76	нет			Аналог: керамогранит ректифицированный под травертин, матовый, 600×600×9 мм; тип 3, отм. ЧП +3,135	6,29	Н стен 2615 (до потолка); гидроизоляция обмазочная, 2 слоя, с заведением на стены 200 мм; у душа — до 2000 и 500 мм за поддон (по пирогу пола); тест проливом и акт скрытых работ; краска бренда веера Little Greene класс по EN 13300 и блеск линейки — по ТУ Little Greene, в базе не сверены
	Итого			**307,27**			**633,37**			**229,8**		**295,89**	

Примечания

1. Площади поверхностей — по чистым граням стен до отделки: стены = периметр × высоту от чистого пола помещения до низа потолка минус проёмы (облицовка плиткой — до верха облицовки); плинтус = периметр минус дверные проёмы; пол и потолок — по площади помещения. Количество плиток по раскладке. Площади помещений — с учётом всех частей помещения; откосы в площадь стен не входят.
2. Акцентные стены и фартук — отдельными строками, их площадь вычтена из основной отделки стен помещения; фартук — над нижними модулями кухни от столешницы до низа навесных шкафов, где шкафов нет — на 600 мм.
3. Плинтус — длина по периметру за вычетом дверных проёмов; примыкания к наличникам и встроенной мебели — по развёрткам.
4. Формат плитки — Ш×В×Т (ширина × высота в положении укладки × толщина), мм; на полу — вдоль стен А/В × вдоль стен Б/Г.
5. Коды цвета — по веерам производителей; колеровка каждой краски одной партией, проверка выкраса при свете D65 и при лампах проекта.
6. Уровни подготовки Q1–Q4 — система Knauf, не норма ГОСТ/СП; допуски поверхностей — по СП 71.13330.2017 (действующая редакция).
7. «аналог:» — изделие задано характеристиками, марку и артикул согласовать с заказчиком до закупки.
8. Плавающая стяжка по звукоизоляции: демпферная (кромочная) лента по контуру помещения и у стояков (СП 51.13330.2011, п. 9.11); плинтус крепится только к стене.
9. Сводка площадей по материалам, м²: потолок — NCS S 0804-Y30R Luja 7 — 49,81; потолок — Little Greene No. 105 Absolute Matt — 202,86; потолок — Little Greene No. 105 Intelligent Bathroom — 20,86; потолок — NCS S 0804-Y30R Anti-Reflex 2 — 33,74; стены — NCS S 0804-Y30R Luja 7 — 113,16; стены — Farrow & Ball No. 226 Modern Emulsion — 325,94; стены — Farrow & Ball No. 298 Modern Emulsion — 5,68; стены — облицовка плиткой 600×1200×9 мм, Atlas Concorde A8UZ — 58,23; стены — NCS S 0804-Y30R Optiva 5 Matt — 32,20; стены — Farrow & Ball No. 93 Modern Emulsion — 12,92; стены — Little Greene No. 105 Intelligent Matt — 41,96; стены — NCS S 7020-G10Y Optiva 5 Matt — 7,60; стены — Farrow & Ball No. 64 Modern Emulsion — 7,35; стены — NCS S 3020-G30Y Optiva 5 Matt — 12,33; стены — NCS S 3040-Y70R Optiva 5 Matt — 14,85; фартук облицовка керамогранитом, #F1F1EC — 1,15.

					Проект: Дом 331 м²
	Лист	№ док.	Подпись	Дата	Ведомость отделки помещений. Лист 4 из 4
Дизайнер	Кырлан А.С.			04.11.26	

Стадия	Лист	Листов
П	С4	168

Поз.	Наименование и техническая характеристика	Тип, марка, обозначение документа	Код продукции	Поставщик	Ед. изм.	Кол.	Образец	Примечание
	Лакокрасочные материалы							
1	Краска интерьерная водно-дисперсионная акриловая для стен, полуматовая, класс мокрого истирания 1 по EN 13300, база A; цвет NCS S 0804-Y30R «S 0804-Y30R», колеровка машинная	Tikkurila Luja 7		Tikkurila	л	30,6		поз. К1 колерной карты; пом. 1, 11, 12; S = 113,2 м² × 2 сл. × 0,12 л/м² = 27,2 л, +10 % и 0,5 л на подкраску → ≥ 30,4 л; тара 3 × 9 л + 1 × 2,7 л + 1 × 0,9 л
2	Краска интерьерная водно-дисперсионная акриловая для потолков, матовая, класс мокрого истирания 1 по EN 13300, база A; цвет NCS S 0804-Y30R «S 0804-Y30R», колеровка машинная	Tikkurila Luja 7		Tikkurila	л	14,4		поз. К2 колерной карты; пом. 1, 11, 12; S = 49,8 м² × 2 сл. × 0,12 л/м² = 12,0 л, +10 % и 0,5 л на подкраску → ≥ 13,6 л; тара 1 × 9 л + 2 × 2,7 л
3	Краска интерьерная водно-дисперсионная акриловая для стен, матовая, класс мокрого истирания 1 по EN 13300, база A; цвет по вееру Farrow & Ball No. 226 «Joa's White», колеровка машинная	Farrow & Ball Modern Emulsion		Farrow & Ball	л	87,5		поз. К4 колерной карты; пом. 2, 4, 6, 8, 9, 10, 13, 16, 17, 18, 19; S = 325,9 м² × 2 сл. × 0,12 л/м² = 78,2 л, +10 % и 0,5 л на подкраску → ≥ 86,5 л; тара 17 × 5 л + 1 × 2,5 л
4	Краска интерьерная водно-дисперсионная акриловая для акцентных стен, матовая, класс мокрого истирания 1 по EN 13300, база C; цвет по вееру Farrow & Ball No. 298 «Bancha», колеровка машинная	Farrow & Ball Modern Emulsion		Farrow & Ball	л	2,5		поз. К5 колерной карты; пом. 2; S = 5,7 м² × 2 сл. × 0,12 л/м² = 1,4 л, +10 % и 0,5 л на подкраску → ≥ 2,0 л; тара 1 × 2,5 л
5	Краска интерьерная водно-дисперсионная акриловая для потолков, глубокоматовая, класс мокрого истирания 2 по EN 13300, база A; цвет по вееру Little Greene No. 105 «Slaked Lime», колеровка машинная	Little Greene Absolute Matt		Little Greene	л	54,1		поз. К6 колерной карты; пом. 2, 4, 6, 7, 8, 9, 10, 13, 14, 16, 17, 18, 19; S = 202,9 м² × 2 сл. × 0,12 л/м² = 48,7 л, +10 % и 0,5 л на подкраску → ≥ 54,1 л; тара — кратно фасовке продукта
6	Краска интерьерная водно-дисперсионная акриловая для потолков, матовая, класс мокрого истирания 1 по EN 13300, база A; цвет по вееру Little Greene No. 105 «Slaked Lime», колеровка машинная	Little Greene Intelligent Bathroom		Little Greene	л	6,1		поз. К8 колерной карты; пом. 3, 15, 20; S = 20,9 м² × 2 сл. × 0,12 л/м² = 5,0 л, +10 % и 0,5 л на подкраску → ≥ 6,0 л; тара — кратно фасовке продукта
7	Краска интерьерная водно-дисперсионная акриловая для стен, матовая, класс мокрого истирания 2 по EN 13300, база A; цвет NCS S 0804-Y30R «S 0804-Y30R», колеровка машинная	Tikkurila Optiva 5 Matt		Tikkurila	л	9,9		поз. К9 колерной карты; пом. 5; S = 32,2 м² × 2 сл. × 0,12 л/м² = 7,7 л, +10 % и 0,5 л на подкраску → ≥ 9,0 л; тара 1 × 9 л + 1 × 0,9 л
8	Краска интерьерная водно-дисперсионная акриловая для акцентных стен, матовая, класс мокрого истирания 1 по EN 13300, база C; цвет по вееру Farrow & Ball No. 93 «Studio Green — почти чёрный зелёный», колеровка машинная	Farrow & Ball Modern Emulsion		Farrow & Ball	л	7,5		поз. К10 колерной карты; пом. 5; S = 12,9 м² × 3 сл. × 0,12 л/м² = 4,7 л, +10 % и 0,5 л на подкраску → ≥ 5,6 л; тара 1 × 5 л + 1 × 2,5 л
9	Краска интерьерная водно-дисперсионная акриловая для потолков, глубокоматовая, класс мокрого истирания 2 по EN 13300, база A; цвет NCS S 0804-Y30R «S 0804-Y30R», колеровка машинная	Tikkurila Anti-Reflex 2		Tikkurila	л	9,9		поз. К11 колерной карты; пом. 5; S = 33,7 м² × 2 сл. × 0,12 л/м² = 8,1 л, +10 % и 0,5 л на подкраску → ≥ 9,4 л; тара 1 × 9 л + 1 × 0,9 л
10	Краска интерьерная водно-дисперсионная акриловая для стен, матовая, класс мокрого истирания 1 по EN 13300, база A; цвет по вееру Little Greene No. 105 «Slaked Lime», колеровка машинная	Little Greene Intelligent Matt		Little Greene	л	11,6		поз. К12 колерной карты; пом. 7, 14; S = 42,0 м² × 2 сл. × 0,12 л/м² = 10,1 л, +10 % и 0,5 л на подкраску → ≥ 11,6 л; тара — кратно фасовке продукта
11	Краска интерьерная водно-дисперсионная акриловая для акцентных стен, матовая, класс мокрого истирания 2 по EN 13300, база C; цвет NCS S 7020-G10Y «Хвойный тёмно-зелёный», колеровка машинная	Tikkurila Optiva 5 Matt		Tikkurila	л	2,7		поз. К14 колерной карты; пом. 13; S = 7,6 м² × 2 сл. × 0,12 л/м² = 1,8 л, +10 % и 0,5 л на подкраску → ≥ 2,5 л; тара 1 × 2,7 л
12	Краска интерьерная водно-дисперсионная акриловая для акцентных стен, матовая, класс мокрого истирания 1 по EN 13300, база C; цвет по вееру Farrow & Ball No. 64 «Red Earth», колеровка машинная	Farrow & Ball Modern Emulsion		Farrow & Ball	л	2,5		поз. К15 колерной карты; пом. 16; S = 7,3 м² × 2 сл. × 0,12 л/м² = 1,8 л, +10 % и 0,5 л на подкраску → ≥ 2,4 л; тара 1 × 2,5 л
13	Краска интерьерная водно-дисперсионная акриловая для акцентных стен, матовая, класс мокрого истирания 2 по EN 13300, база C; цвет NCS S 3020-G30Y «S 3020-G30Y», колеровка машинная	Tikkurila Optiva 5 Matt		Tikkurila	л	4,5		поз. К16 колерной карты; пом. 18; S = 12,3 м² × 2 сл. × 0,12 л/м² = 3,0 л, +10 % и 0,5 л на подкраску → ≥ 3,8 л; тара 1 × 2,7 л + 2 × 0,9 л
14	Краска интерьерная водно-дисперсионная акриловая для акцентных стен, матовая, класс мокрого истирания 2 по EN 13300, база C; цвет NCS S 3040-Y70R «S 3040-Y70R», колеровка машинная	Tikkurila Optiva 5 Matt		Tikkurila	л	4,5		поз. К18 колерной карты; пом. 19; S = 14,8 м² × 2 сл. × 0,12 л/м² = 3,6 л, +10 % и 0,5 л на подкраску → ≥ 4,4 л; тара 1 × 2,7 л + 2 × 0,9 л
15	Акрилово-уретановая эмаль на водной основе, полуглянцевая в цвет NCS S 0804-Y30R «S 0804-Y30R» — окраска плинтуса	аналог по характеристикам			л	1		поз. К3; пом. 1, 5; L = 36,5 м, S = 3,5 м² × 2 сл. × 0,12 л/м² + 10 %; продукт подобрать в веере NCS
16	Краска для МДФ и дерева в цвет Farrow & Ball No. 226 «Joa's White» — окраска плинтуса; блеск не ниже блеска стен	марка не задана			л	3,2		поз. К7, К17; пом. 2, 4, 6, 8, 9, 13, 16, 17, 18, 19; L = 127,7 м, S = 11,9 м² × 2 сл. × 0,12 л/м² + 10 %; продукт подобрать в веере Farrow & Ball
17	Краска для МДФ и дерева в цвет Little Greene No. 105 «Slaked Lime» — окраска плинтуса; блеск не ниже блеска стен	марка не задана			л	0,5		поз. К13; пом. 7, 14; L = 16,8 м, S = 1,6 м² × 2 сл. × 0,12 л/м² + 10 %; продукт подобрать в веере Little Greene
18	Грунтовка акриловая под окраску стен и потолков — из системы производителя краски	по системе краски			м²	882		площадь окраски стен, акцентов и потолков; 1 слой перед окраской; расход — по ТУ грунтовки

					Проект: Дом 331 м²
	Лист	№ док.	Подпись	Дата	
Дизайнер	Кырлан А.С.			04.11.26	Спецификация отделочных материалов
					Стадия: П; Лист: С5; Листов: 168

Поз.	Наименование и техническая характеристика	Тип, марка, обозначение документа	Код продукции	Поставщик	Ед. изм.	Кол.	Образец	Примечание
	Плитка и керамогранит							
19	Керамогранит под травертин, 600×600×9 мм, ректификат, водопоглощение 0,1 % (BIa), противоскольжение R10, PEI IV	аналог по характеристикам			м²	22,32		шов 2 мм; Санузел 1 этажа, пол; Санузел мастер, пол; Санузел 2, пол; по раскладке 56 шт (S = 18,04 м²), с запасом 62 шт
20	A8UZ, 600×1200×9 мм, ректификат, водопоглощение 0,1 % (BIa), противоскольжение R10, PEI IV	A8UZ		Atlas Concorde	м²	163,44		шов 2 мм; Санузел 1 этажа, стены А–Г; Санузел 1 этажа, короб инсталляции; Санузел мастер, стены А–Г; Санузел мастер, короб инсталляции; Санузел 2, стены А–Г; Санузел 2, короб инсталляции; Котельная, пол; Прихожая, пол; Тамбур, пол; Веранда, пол; Крыльцо, пол; по раскладке 202 шт (S = 108,61 м²), с запасом 227 шт
21	Керамогранит матовый, тон F497, ректификат, водопоглощение 0,5 % (BIa)	аналог по характеристикам			м²	1,26		1. Кухня-столовая, фартук; раскладка не выполнена — S = 1,15 м² + 10 %; клей и затирка — по раскладке
22	Плинтус из керамогранита пола, подрезка 80 мм, верхняя кромка с запилом 45°	аналог по характеристикам			м²	22,53		11. Веранда, стены; раскладка не выполнена — S = 20,48 м² + 10 %; клей и затирка — по раскладке
23	Плинтус из керамогранита пола, подрезка 80 мм, верхняя кромка с запилом 45°	аналог по характеристикам			м²	7		12. Крыльцо, стены; раскладка не выполнена — S = 6,36 м² + 10 %; клей и затирка — по раскладке
	Напольные покрытия							
24	1167-4250, рабочий слой 4 мм, эмиссия E1, укладка на клей	1167-4250		Coswick	м²	201,4		пом. 1, 2, 5, 6, 7, 13, 14, 16, 17, 18, 19; S = 188,22 м² + 7 % (прямая укладка); к заказу — кратно упаковке
25	Клей для паркета и инженерной доски, эластичный (СМП / полиуретановый)	по рекомендации производителя доски			м²	189		площадь приклейки; расход и шпатель — по ТУ клея
	Погонажные изделия							
26	Плинтус МДФ под окраску 80×16 мм, крепление к стене, окраска в цвет NCS S 0804-Y30R	аналог по характеристикам			м	41		пом. 1, 5; L = 36,5 м (периметр без дверных проёмов) + 10 % на подрезку; в штуках — по длине планки
27	Плинтус МДФ под покраску 80×16, крепление к стене, окраска в цвет Farrow & Ball No. 226	аналог по характеристикам			м	106		пом. 2, 4, 6, 8, 9, 13, 16, 17; L = 95,5 м (периметр без дверных проёмов) + 10 % на подрезку; в штуках — по длине планки
28	Плинтус МДФ под покраску 80×16, крепление к стене, окраска в цвет Little Greene No. 105	аналог по характеристикам			м	19		пом. 7, 14; L = 16,8 м (периметр без дверных проёмов) + 10 % на подрезку; в штуках — по длине планки
29	Плинтус ПВХ влагостойкий 100 мм, серый, h = 100 мм, крепление к стене	аналог по характеристикам			м	25		пом. 10; L = 22,0 м (периметр без дверных проёмов) + 10 % на подрезку; в штуках — по длине планки
30	Плинтус из керамогранита пола, подрезка 80 мм, верхняя кромка с запилом 45°, h = 80 мм, крепление к стене	аналог по характеристикам			м	30		пом. 11, 12; L = 26,8 м (периметр без дверных проёмов) + 10 % на подрезку; в штуках — по длине планки
31	SX165, h = 69 мм, крепление к стене, окраска в цвет Farrow & Ball No. 226	SX165		Orac Decor	м	36		пом. 18, 19; L = 32,2 м (периметр без дверных проёмов) + 10 % на подрезку; в штуках — по длине планки
	Смеси и материалы для облицовки							
32	Затирка для швов плитки, класс CG2WA по EN 13888	Mapei Ultracolor Plus 132		Mapei	кг	11		по раскладке (a+b)/(a·b) × шов × t × 1,6 + 10 %; в т. ч. 3,9 кг — позиции раскладки без марки
33	Клей плиточный C2 TE S1 по EN 12004, слой 5 мм	Ceresit CM 17		Ceresit	кг	1080		44 меш. по 25 кг; 1,5 кг/м² на 1 мм слоя + 10 %; в т. ч. 389 кг — позиции раскладки без марки
34	Гидроизоляция обмазочная мокрых зон: пол, стены по периметру, зоны замачивания; 2 слоя с армирующей лентой в углах	аналог по характеристикам			м²	44,9		площадь по листу раскладки плитки + 10 %; расход смеси — по ТУ
35	Лента демпферная по периметру пола из плитки	аналог по характеристикам			м	90,5		периметр без дверных проёмов + 10 %

Примечания

1. Количества — из геометрии проекта: площади поверхностей по чистым граням стен до отделки (те же, что в ведомости отделки и колерной карте), плитка, клей и затирка — по раскладке плиточника; в графе «Кол.» — к заказу, с запасом.
2. Краска: расход 0,12 л/м² на слой в 2 слоя, если по ТУ не задан иной; запас 10 % и 0,5 л на подкраску каждого кода. Один код — одна партия, колеровка машинная в колеровочном центре бренда; в заказ — только после утверждения выкраса (колерная карта). Фасовка — по каталогу бренда на дату выпуска; к заказу — не меньше расчётного объёма.
3. «Аналог по характеристикам» — допускается изделие другого производителя с характеристиками не ниже указанных, по согласованию с автором проекта.
4. Графы «Код продукции» и «Масса 1 ед.» не заполнены: коды по классификатору продукции не присвоены, масса единицы до 25 кг (ГОСТ 21.110-2013).
5. Грунтовка и клей для доски указаны площадью обработки; объём — по ТУ выбранного продукта.

					Проект: Дом 331 м²
	Лист	№ док.	Подпись	Дата	Спецификация отделочных материалов
Дизайнер	Кырлан А.С.			04.11.26	

Стадия	Лист	Листов
П	С6	168

Список покупок: материалы для магазина

№	Что купить	Артикул или характеристика	Нужно с запасом	Брать в магазине	Фасовка	Уточнить в магазине	Помещения	Кто покупает
Покрытия полов и облицовка								
1	Инженерная доска (дуб натуральный, рабочий слой 4 мм, эмиссия E1, прямая укладка)	1167-4250	203,37 м²	203,4 м²		уточнить в магазине: м² в упаковке	1, 2, 5, 6, 7, 13, 14, 16, 17, 18, 19	по проекту
2	Клей для паркетной и инженерной доски (эластичный, по ТУ изготовителя доски)	на выбор бригады по проекту	190,07 м²			уточнить в магазине: расход и фасовку — по выбранному продукту		бригада
3	Керамогранит 600×600 мм под травертин	по характеристике: керамогранит под травертин	62 шт	62 шт		уточнить в магазине: штук в коробке	3, 15, 20	по проекту
4	Керамогранит 600×1200 мм A8UZ	A8UZ	223 шт	227 шт		уточнить в магазине: штук в коробке	3, 4, 8, 9, 11, 12, 15, 20	по проекту
Сухие смеси и гидроизоляция								
5	Клей плиточный цементный класса C2 TE S1 (ГОСТ Р 56387-2018)	Ceresit CM 17 или аналог	1079,12 кг	44 меш.	мешок 25 кг			по проекту
6	Затирка цементная класса CG2WA, цвет — по колерной карте	Mapei Ultracolor Plus 132 или аналог	11,01 кг	6 упак.	упак. 2 кг			по проекту
7	Гидроизоляция обмазочная полимерная, 2 слоя, лента в углах, манжеты на выводах	на выбор бригады по проекту	44,92 м²			уточнить в магазине: расход и фасовку — по выбранному продукту	3, 15, 20	бригада
8	Лента демпферная по периметру пола из плитки	на выбор бригады по проекту	90,46 м	91 м		уточнить в магазине: фасовку		бригада
9	Смесь цементно-песчаная для стяжки М200 (47 мм, 50 мм, 33 мм, 49 мм, 61 мм)	на выбор бригады по проекту	14,43 м³			уточнить в магазине: расход и фасовку — по выбранному продукту		бригада
10	Смесь штукатурная гипсовая для машинного и ручного нанесения по маякам, слой до 10 мм	на выбор бригады по проекту	741,66 м²			уточнить в магазине: расход и фасовку — по выбранному продукту	1, 2, 3, 4, 5, 6, 7, 8, 9, 10, 11, 12, 13, 14, 15, 16, 17, 18, 19, 20	бригада
Короба из ГКЛВ								
11	Лист ГКЛВ 12,5 мм, 2500 × 1200 мм, обшивка коробов в 2 слоя	на выбор бригады по проекту	10,65 м²	4 лист.	лист 3,00 м²		3, 15, 20	бригада
12	Профиль стальной оцинкованный 27 × 28 мм: каркас коробов (стойки и направляющие)	на выбор бригады по проекту	26,38 м	9 шт	хлыст 3 м			бригада
Слаботочные сети								
13	Кабель домофона — тип по системе поставщика	на выбор бригады по проекту	2,8 м	3 м		уточнить в магазине: длину бухты		бригада
14	Кабель коаксиальный RG-6 (75 Ом) к розеткам ТВ	на выбор бригады по проекту	70,6 м	71 м		уточнить в магазине: длину бухты		бригада
15	Кабель U/UTP кат. 5e (LAN, Wi-Fi и камеры по PoE)	на выбор бригады по проекту	11,9 м	12 м		уточнить в магазине: длину бухты		бригада
16	Кабель U/UTP кат. 6 (LAN, Wi-Fi и камеры по PoE)	на выбор бригады по проекту	96,4 м	97 м		уточнить в магазине: длину бухты		бригада
17	Гофротруба Ø20 для слаботочных линий, отдельно от силовых	на выбор бригады по проекту	163,5 м	164 м		уточнить в магазине: длину бухты		бригада
18	Розетка компьютерная RJ45, кат. 6, с рамкой и подрозетником	на выбор бригады по проекту	7 шт	7 шт	шт			бригада
19	Розетка телевизионная (коаксиальная) с рамкой и подрозетником	на выбор бригады по проекту	5 шт	5 шт	шт			бригада
20	Трубка или монитор домофона (поставка домофонной организации)	на выбор бригады по проекту	1 шт	1 шт	шт			по проекту
21	Щит слаботочный ЩС: корпус, DIN-рейка, розетки 220 В	на выбор бригады по проекту	1 шт	1 шт	шт			бригада
22	Патч-панель, портов не менее 8	на выбор бригады по проекту	1 шт	1 шт	шт			бригада
Лакокрасочные материалы								
23	Краска интерьерная акриловая, полуматовая, класс истирания 1	Tikkurila Luja 7 S 0804-Y30R «S 0804-Y30R»	30,17 л	12 банк.	банка 2,7 л		1, 11, 12	по проекту
24	Краска интерьерная акриловая, матовая, класс истирания 1	Tikkurila Luja 7 S 0804-Y30R «S 0804-Y30R»	13,15 л	5 банк.	банка 2,7 л		1, 11, 12	по проекту

					Проект: Дом 331 м²
	Лист	№ док.	Подпись	Дата	
Дизайнер	Кырлан А.С.			04.11.26	Список покупок

Стадия	Лист	Листов
П	С7	168

Список покупок: материалы для магазина (продолжение)

№	Что купить	Артикул или характеристика	Нужно с запасом	Брать в магазине	Фасовка	Уточнить в магазине	Помещения	Кто покупает
25	Краска интерьерная акриловая, матовая, класс истирания 1	Farrow & Ball Modern Emulsion No. 298 «Bancha»	1,5 л	1 банк.	банка 2,5 л		2	по проекту
26	Краска интерьерная акриловая, матовая, класс истирания 1	Farrow & Ball Modern Emulsion No. 226 «Joa's White»	86,05 л	35 банк.	банка 2,5 л		2, 4, 6, 8, 9, 10, 13, 16, 17, 18, 19	по проекту
27	Краска интерьерная акриловая, глубокоматовая, класс истирания 2	Little Greene Absolute Matt No. 105 «Slaked Lime»	51,29 л	51,3 л		уточнить в магазине: объём банки	2, 4, 6, 7, 8, 9, 10, 13, 14, 16, 17, 18, 19	по проекту
28	Краска интерьерная акриловая, матовая, класс истирания 1	Little Greene Intelligent Bathroom No. 105 «Slaked Lime»	4,76 л	4,8 л		уточнить в магазине: объём банки	3, 15, 20	по проекту
29	Краска интерьерная акриловая, матовая, класс истирания 1	Farrow & Ball Modern Emulsion No. 93 «Studio Green — почти чёрный зелёный»	5,12 л	3 банк.	банка 2,5 л		5	по проекту
30	Краска интерьерная акриловая, матовая, класс истирания 2	Tikkurila Optiva 5 Matt S 0804-Y30R «S 0804-Y30R»	8,5 л	4 банк.	банка 2,7 л		5	по проекту
31	Краска интерьерная акриловая, глубокоматовая, класс истирания 2	Tikkurila Anti-Reflex 2 S 0804-Y30R «S 0804-Y30R»	8,91 л	4 банк.	банка 2,7 л		5	по проекту
32	Краска интерьерная акриловая, матовая, класс истирания 1	Little Greene Intelligent Matt No. 105 «Slaked Lime»	11,08 л	11,1 л		уточнить в магазине: объём банки	7, 14	по проекту
33	Краска интерьерная акриловая, матовая, класс истирания 2	Tikkurila Optiva 5 Matt S 7020-G10Y «Хвойный тёмно-зелёный»	2 л	1 банк.	банка 2,7 л		13	по проекту
34	Краска интерьерная акриловая, матовая, класс истирания 1	Farrow & Ball Modern Emulsion No. 64 «Red Earth»	1,94 л	1 банк.	банка 2,5 л		16	по проекту
35	Краска интерьерная акриловая, матовая, класс истирания 2	Tikkurila Optiva 5 Matt S 3020-G30Y «S 3020-G30Y»	3,26 л	2 банк.	банка 2,7 л		18	по проекту
36	Краска интерьерная акриловая, матовая, класс истирания 2	Tikkurila Optiva 5 Matt S 3040-Y70R «S 3040-Y70R»	3,92 л	2 банк.	банка 2,7 л		19	по проекту
37	Шпаклёвка финишная полимерная под окраску (стены и потолки, Q3)	на выбор бригады по проекту	986,99 м²			уточнить в магазине: расход и фасовку — по выбранному продукту		бригада
38	Грунтовка акриловая глубокого проникновения, 2 слоя	на выбор бригады по проекту	1067,14 м²			уточнить в магазине: расход и фасовку — по выбранному продукту		бригада
Погонажные изделия и потолки								
39	Плинтус напольный МДФ под покраску, h=80 мм, крепление к стене	по характеристике: плинтус МДФ под окраску 80×16 мм	40,15 м.п.	17 шт	хлыст 2,4 м		1, 5	по проекту
40	Плинтус напольный МДФ под покраску, h=80 мм, крепление к стене	по характеристике: плинтус МДФ под покраску 80×16	123,53 м.п.	52 шт	хлыст 2,4 м		2, 4, 6, 7, 8, 9, 13, 14, 16, 17	по проекту
41	Плинтус напольный ПВХ, h=100 мм, крепление к стене	по характеристике: плинтус ПВХ влагостойкий 100 мм, серый	24,18 м.п.	11 шт	хлыст 2,4 м		10	по проекту
42	Керамогранит на плинтус: полосы h=80 мм из плитки пола, кромка с запилом 45°	по характеристике: плинтус из керамогранита пола, подрезка 80 мм, верхняя кромка с запилом 45°	2,47 м²	2,47 м²		уточнить в магазине: м² в коробке	11, 12	по проекту
43	Плинтус напольный МДФ под покраску, h=69 мм, крепление к стене	SX165	35,42 м.п.	15 шт	хлыст 2,4 м		18, 19	по проекту
44	Потолок подвесной ГКЛ/ГКЛВ по каркасу Knauf П113: листы, профили, подвесы, лента, шпаклёвка швов	Knauf П113	202,89 м²			уточнить в магазине: расход и фасовку — по выбранному продукту		по проекту


Примечания

1. «Нужно с запасом» — расход по чертежам и раскладке плюс запас на подрезку и подкраску; «Брать в магазине» — то же количество в единицах, которыми продают (банки, мешки, упаковки, листы, штуки, литры).
2. «Уточнить в магазине» — фасовки этого товара в проекте нет: спросите у продавца, сколько в упаковке, и возьмите целое число упаковок не меньше «Нужно с запасом».
3. Плитку, доску и краску одного цвета берите одной партией (один калибр и тон на помещение) и сохраните чек и номер партии до конца ремонта.
4. «По характеристике» — артикул не выбран: подойдёт любой товар с этими свойствами, согласуйте его с дизайнером до покупки. «Бригада» материал выбирает и закупает бригада по своей технологии.
5. Помещения: 1 — Кухня-столовая; 2 — Кабинет-гостевая; 3 — Санузел 1 этажа; 4 — Котельная; 5 — Гостиная; 6 — Холл с лестницей; 7 — Кладовая; 8 — Прихожая; 9 — Тамбур; 10 — Гараж; 11 — Веранда; 12 — Крыльцо; 13 — Спальня мастер; 14 — Гардеробная мастер; 15 — Санузел мастер; 16 — Спальня 2; 17 — Холл мансарды; 18 — Спальня 3; 19 — Спальня 4; 20 — Санузел 2; «—» — материал для нескольких помещений, расход по месту.

					Проект: Дом 331 м²
	Лист	№ док.	Подпись	Дата	
Дизайнер	Кырлан А.С.			04.11.26	Список покупок (окончание)
					Стадия: П; Лист: С8; Листов: 168


1 Порог 15 мм: мокрая зона — смежное помещение (М 1:5)

Применение: двери Д-2, Д-9, Д-13

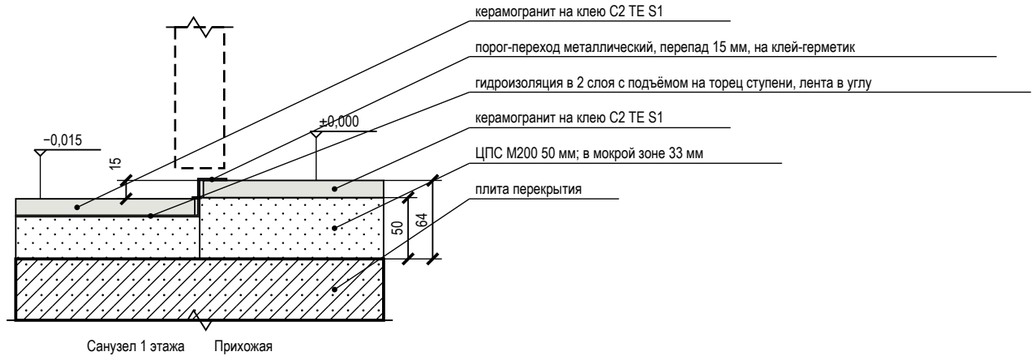


2 Стык покрытий пола с перепадом 30 мм, профиль-переход (М 1:5)

Применение: проёмы 5↔11

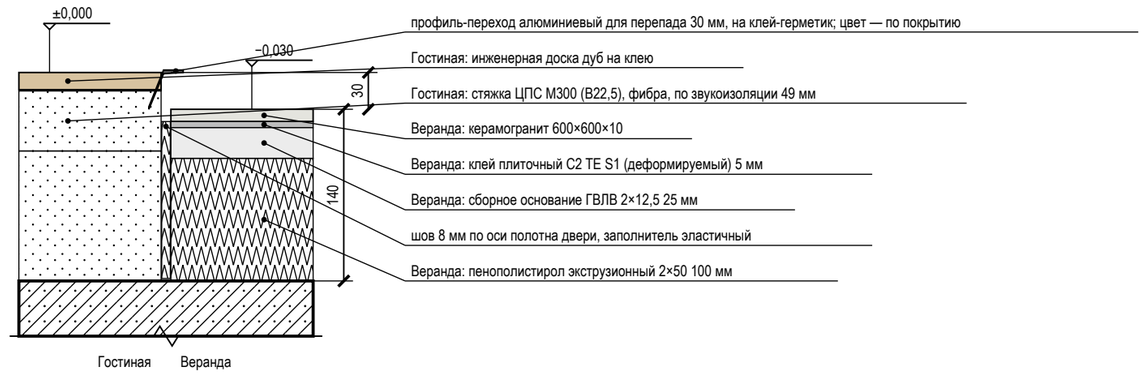


3 Дверь скрытого монтажа в плоскости стены, плинтус (М 1:5)

Применение: двери Д-1, Д-2, Д-7, Д-8, Д-9, Д-10, Д-11, Д-12, Д-13

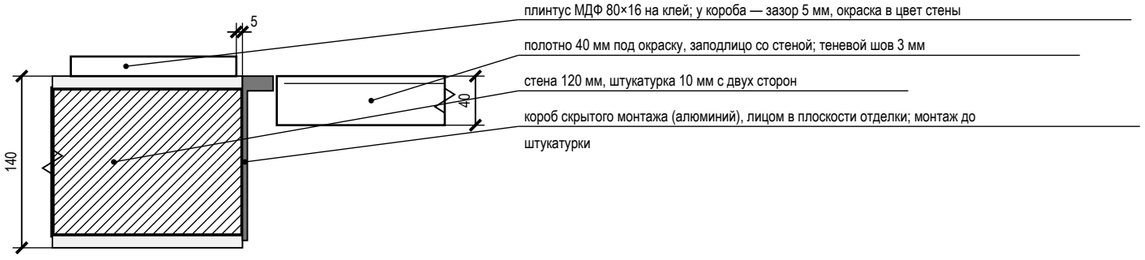

4 Короб стояков К1-1 с люком и звукоизоляцией (М 1:10)

Применение: пом. 3, 1, 8

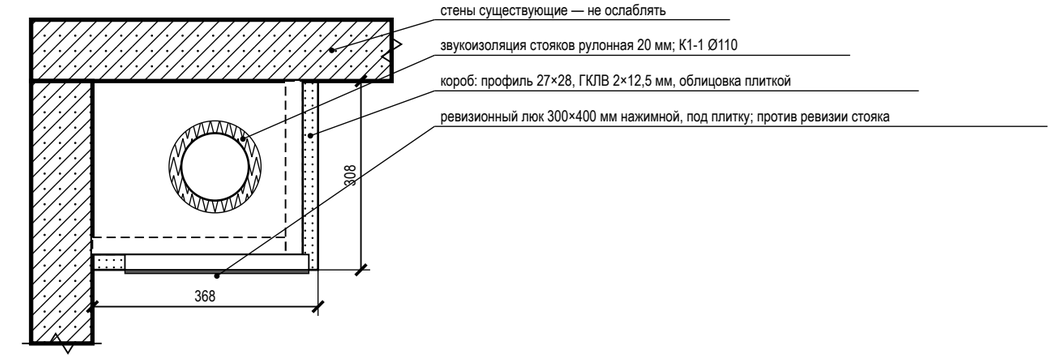

Условные обозначения

- железобетон (плита, стены) — условно: конструкция не установлена
- кладка, перегородка — условно: конструкция не установлена
- стяжка, раствор
- гипсокартон ГКЛВ
- звукоизоляция, эластичный заполнитель
- плитка, керамогранит на клею
- инженерная доска (покрытие пола)
- металлический профиль (порог, Т-профиль, короб двери)
- гидроизоляция (обмазочная, лента)

Примечания


1. Узлы — типовые решения проекта для мест, отмеченных выносками на листе схемы расположения развёрток и узлов; размеры — в мм, отметки — в м от ±0,000 (чистый пол 1-го этажа).
2. Узлы с гидроизоляцией, закладными и коробами скрытого монтажа принимаются по актам скрытых работ до закрытия отделкой; гидроизоляция — после теста проливом (24 ч).
3. Марки изделий (порог, Т-профиль, короб скрытой двери, люк) — по спецификациям; замена — на аналог с теми же габаритами по согласованию с автором проекта.
4. Материал плиты перекрытия и стен в узлах показан условно (железобетон, кладка): конструкция дома не установлена — крепёж, анкеры и толщины слоёв уточняются после обследования (до него — по допущениям общих указаний).
5. Узел 1 применяется на этажах: 1-й этаж, Мансарда; отметки показаны для пом. 8 (1-й этаж), на этаже «Мансарда» — с поправкой +3,150 (разность отметок чистого пола этажей).
6. Узлы комплекта выпущены на 2 листах, нумерация узлов сквозная: 1–4 — лист С9 альбома (данный лист); 5–8 — лист С10 альбома.

					Проект: Дом 331 м²
	Лист	№ док.	Подпись	Дата	
Дизайнер	Кырлан А.С.			04.11.26	Узлы. Лист 1 из 2

Стадия	Лист	Листов
П	С9	168


5 Гидроизоляция санузла: заход на стены 200 мм, примыкание ванны (М 1:10)

Применение: пом. 3, 15, 20

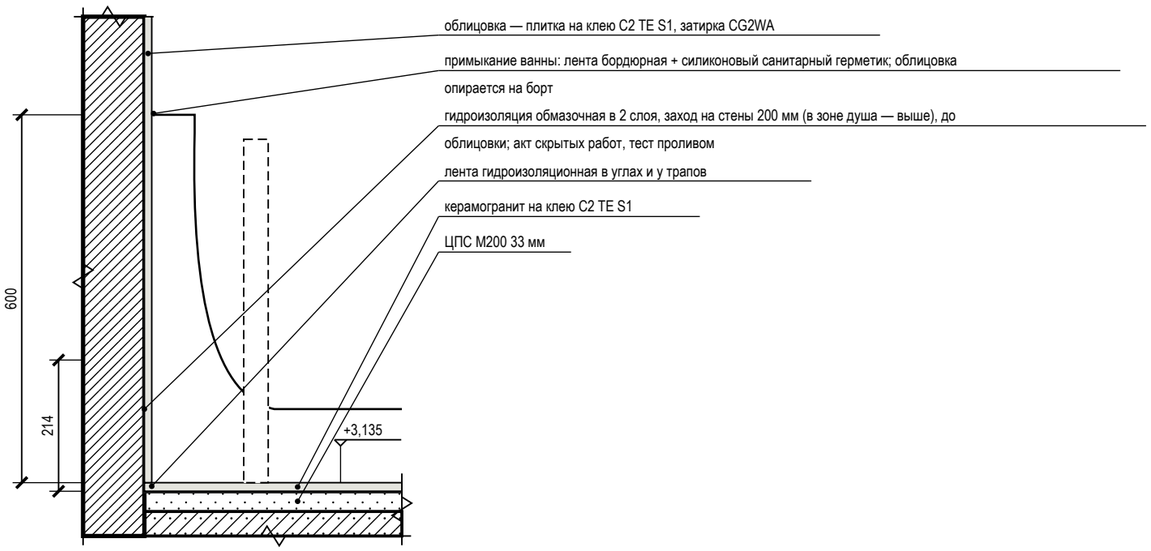


6 Плинтус МДФ 80×16 мм у окрашенной стены по доске (ламинату) (М 1:5)

Применение: пом. 1, 2, 5, 6, 7, 13, 14, 16, 17, 18, 19

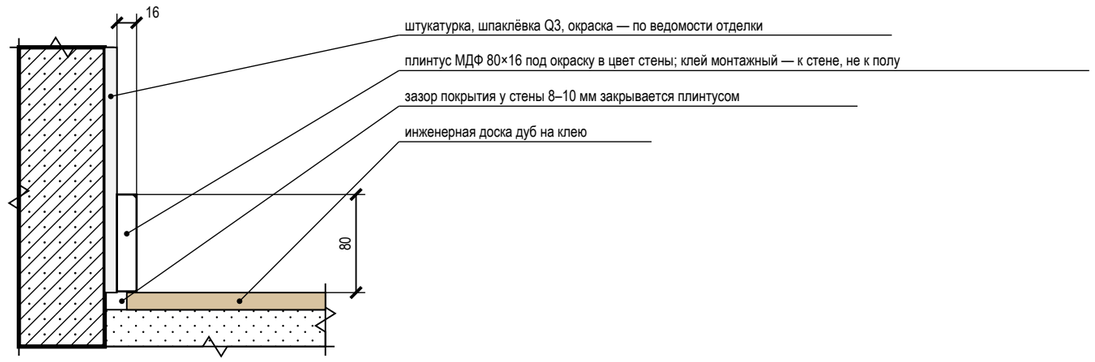


7 Плинтус МДФ 80×16 мм у окрашенной стены по керамограниту (плитке) (М 1:5)

Применение: пом. 4, 8, 9

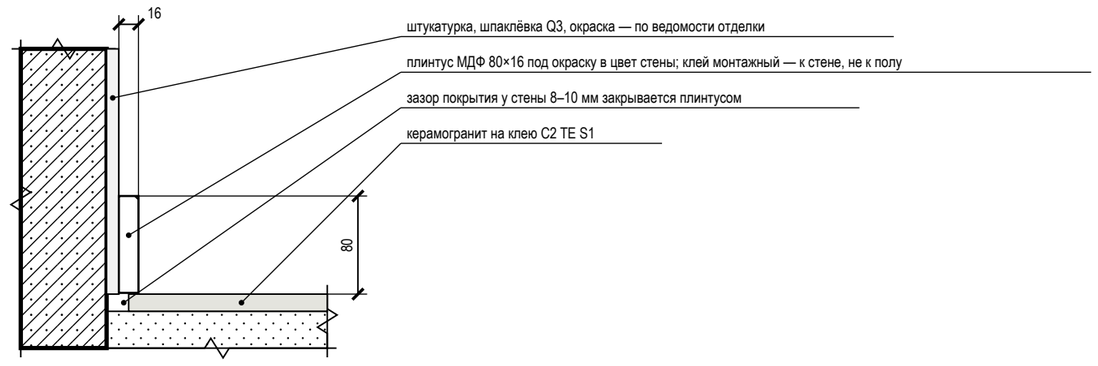

8 Плинтус ПВХ 100×16 мм у окрашенной стены по наливному полу (М 1:5)

Применение: пом. 10

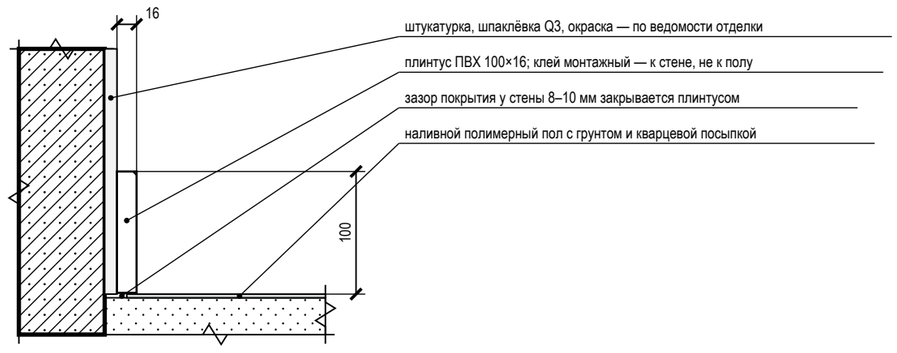

Условные обозначения

- железобетон (плита, стены) — условно: конструкция не установлена
- кладка, перегородка — условно: конструкция не установлена
- стяжка, раствор
- плитка, керамогранит на клею
- инженерная доска (покрытие пола)
- гидроизоляция (обмазочная, лента)

Примечания

1. Узлы — типовые решения проекта для мест, отмеченных выносками на листе схемы расположения развёрток и узлов; размеры — в мм, отметки — в м от ±0,000 (чистый пол 1-го этажа).
2. Узлы с гидроизоляцией, закладными и коробами скрытого монтажа принимаются по актам скрытых работ до закрытия отделкой; гидроизоляция — после теста проливом (24 ч).
3. Марки изделий (порог, Т-профиль, короб скрытой двери, люк) — по спецификациям; замена — на аналог с теми же габаритами по согласованию с автором проекта.
4. Материал плиты перекрытия и стен в узлах показан условно (железобетон, кладка): конструкция дома не установлена — крепёж, анкеры и толщины слоёв уточняются после обследования (до него — по допущениям общих указаний).
5. Узел 5 применяется на этажах: 1-й этаж, Мансарда; отметки показаны для пом. 15 (Мансарда), на этаже «1-й этаж» — с поправкой −3,150 (разность отметок чистого пола этажей).
6. Узлы комплекта выпущены на 2 листах, нумерация узлов сквозная: 1–4 — лист С9 альбома; 5–8 — лист С10 альбома (данный лист).

					Проект: Дом 331 м²
	Лист	№ док.	Подпись	Дата	Узлы. Лист 2 из 2
Дизайнер	Кырлан А.С.			04.11.26	

Стадия	Лист	Листов
П	С10	168

выпуск 04.11.2026 № f163a372b2 · стр. 168 из 168