
LINEA

ДИЗАЙН-ПРОЕКТ ИНТЕРЬЕРА

Трёхкомнатная квартира

Warm Contemporary

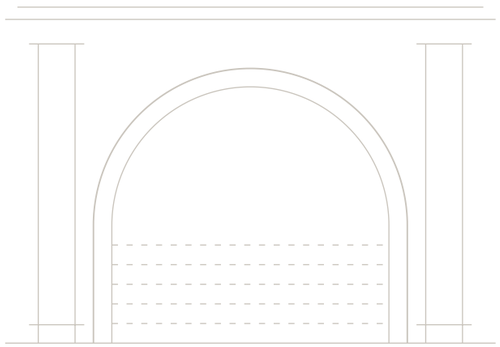

ПАЛИТРА ОТДЕЛКИ

F&B No. 241	V503	F&B No. 30	H487	NCS S 3005-Y20
47 %	37 %	15 %	текстиль, декор	текстиль, декор

АВТОР ПРОЕКТА

Кырлан Александр Сергеевич

Ноябрь 2026



План расстановки мебели · М 1:75

ОБЩАЯ ПЛОЩАДЬ	ПОМЕЩЕНИЙ	СТАДИЯ	ШИФР	ОСНОВА
78,95 м²	8, из них жилых 3	Проект · предварительно	ГД-2026-003-АИ	план заказчика, без обмера

Как оставить правку: кнопка «Правка к этому листу» в правом верхнем углу любого листа · все листы проекта: дизайн-студия-квартир.рф/review.html?p=gost-kv3k

Объект

Трёхкомнатная квартира: 78,95 м², помещений 8, из них жилых 3.

Стиль: современный (контемпорари) 100 %. Стадия: предварительный альбом без обмера, планировка по плану заказчика.

Открытых вопросов 27, конфликтов разделов 0; изменений утверждено 12, ждут подписи 6.

Розетки и выводы

39 розеток (рамок 34), 7 выводов кабеля под технику и свет, 14 групп щита — всё с высотами от чистого пола: листы 34, 35.

Что решено (подписано вами)

ИЗ-1 — Добавлены электрические полотенцесушители IP44: С_04 в ванной (480 мм, низ 900 мм) и С_09 в санузле 2 (400 мм, низ 900 мм), выводы ЭВ6 и ЭВ7.

ИЗ-2 — Стяжка 33 мм и слой обмазочной гидроизоляции 2 мм (2 слоя, заведение на стены 200 мм).

ИЗ-3 — В выключателях S11 и S12 добавлены светорегуляторы (тип te).

ИЗ-4 — Розетка Р33 на высоте 1100 мм, вне шва плитки.

ИЗ-5 — Добавлена вытяжка над варочной панелью М_24 (600 × 400 × 600 мм, низ 1600 мм).

ИЗ-7 — Задана сборка стоя на месте (assembly: in-place): готовый корпус не поднять.

ИЗ-8 — Добавлены выводы к вентиляторам: ЭВ4 (ВР1, ванная) и ЭВ5 (ВР3, санузел 2) — группа 3, высота 2389 мм, включение с основным светом, таймер выбега в вентиляторе.

ИЗ-9 — Р7, Р8 и Р33 на высоте 1000 мм — верхний предел нормы (ПУЭ, п. 6.6.30, не выше 1 м).

ИЗ-10 — Принята норма ПУЭ (п. 7.1.48): розетки в зоне 3 помещения с ванной или душем допустимы при защите УЗО 30 мА.

и ещё 3 — на листе реестра

Что ждёт вашего ответа

К-1 — Ванная (2250 × 1970 мм): после утверждения стиральной машины с вертикальной загрузкой 400 × 600 мм замечания по дверце машины и боковому зазору унитаза С_02 сняты.

К-2 — Артикул плитки и калибр партии (фактический размер плитки) для ванной и санузла 2 не заданы: раскладка рассчитана по номинальным размерам — пол 600 × 600 мм, стены 600 × 1200 мм.

К-3 — Доли цвета по поверхностям не укладываются в схему 60/30/10 и её варианты: ведущий цвет занимает 33 % в спальне 1, 38 % в спальне 2 и 32 % в кухне-гостиной (нужно от 50 %).

К-4 — Вход в санузел 2 (с унитазом) — из кухни-гостиной: так по плану заказчика (ниша у входа на плане открыта в кухню-гостиную, в проекте закрыта перегородкой по линии низа прихожей).

К-5 — Санузел 2 (1675 × 1580 мм): перед душем С_06 до противоположной стены 630 мм (нужно 750).

К-7 — Розетки выше 1 м от пола (норма ПУЭ, п. 6.6.30 — не выше 1 м).

К-8 — Проект кухни не утверждён заказчиком: выводы кухонной техники (мойка М_20, посудомоечная М_21, варочная панель и духовой шкаф М_22, вытяжка М_24, холодильник М_19) приняты по…

К-9 — Гардеробная состоит из двух частей.

К-11 — Высота потолка 2700 мм принята: на плане заказчика она не указана.

К-12 — Две конструкции плана заказчика не определены: утолщение стены 190 × 1360 мм в гардеробной у спальни 2 (вентблок или пилон) и элемент 1470 × 160 мм на линии простенка…

К-13 — Размеры сняты со скана плана заказчика по размерным цепочкам, контрольный обмер на объекте не выполнялся.

К-14 — Разрешённая мощность 15 кВт принята по типовой квартире, технических условий в материалах объекта нет.

К-15 — Графы «Пров.» и «Н. контр.» в штампе пусты: их заполняет человек, подписи проверяющего и нормоконтролёра разработчик проекта не ставит.

К-16 — Сдача разделов специалистами для этого проекта не оформлена (нет файлов решений по ролям).

и ещё 13 — на листе реестра

Предложено, ждёт подписи

ИЗ-6 — Марки: мебель М (кухня ОБ_03, М_15, М_16, М_17, М_18, М_19, М_20, М_22, М_23, М_21, шкафы М_13 и М_14), декор ДК1…ДК9.

ИЗ-14 — Принята типовая схема частного ремонта: материалы и оборудование покупает заказчик по спецификациям проекта.

ИЗ-15 — Р7 на стене Б со смещением 985 мм (на 300 мм дальше вдоль стены, по-прежнему у стиральной машины ОБ_01.

ИЗ-16 — Один источник габарита (plumbing-engineer/sheets/shaft-geom.js): внутренний 195 × 406 мм (трубы Ст К1-1 Ø110 и Ст В1-1 Ø32, изоляция 20 мм, просвет 40 мм, считая от стен угла),…

ИЗ-17 — Слаботочка остаётся: щит слаботочный ЩС в Прихожей (стена Г, 3350 мм от угла, высота 1700 мм, рядом со щитом ЩК.

					Проект: Трёхкомнатная квартира
	Лист	№ док.	Подпись	Дата	Ваш проект на одной странице
Дизайнер	Кырлан А.С.			04.11.26	

Стадия	Лист	Листов
П	2	92

Список листов

Лист	Наименование
1	Титульный лист
2	Ваш проект на одной странице
3	Список листов
4	Как читать альбом
5	План планировки от заказчика
6	План монтажный
7	Схема каркаса перегородки П-1
8	Кухня (пом. 6). Монтажная схема
9	Шкафы. Монтажная схема
10	Карта покрытий стен
11	Колерная карта
12	План размещения мебели и оборудования
13	Спецификация мебели и оборудования
14	Спецификация мебели и оборудования (продолжение)
15	Спецификация мебели и оборудования (продолжение)
16	Ведомости изделий, техники и фурнитуры
17	План выводов сантехники
18	Схема разводки водопровода и канализации
19	Аксонометрическая схема В1 (холодное водоснабжение)
20	Аксонометрическая схема Т3 (горячее водоснабжение)
21	Аксонометрическая схема К1 (канализация)
22	Развёртки мокрых зон: выводы ВК. Ванная (лист 1 из 2)
23	Развёртки мокрых зон: выводы ВК. Ванная (лист 2 из 2)
24	Развёртки мокрых зон: выводы ВК. Кухня-гостиная
25	Развёртки мокрых зон: выводы ВК. Санузел 2
26	Спецификация сантехнического оборудования
27	Раскладка плитки. Ванная. Развёртки стен
28	Раскладка плитки. Санузел 2. Развёртки стен
29	План размещения дверей
30	План потолков
31	Разрезы и узлы потолков
32	Разрезы и узлы потолков (продолжение)
33	Сечения потолков М 1:10
34	Однолинейная схема щита
35	План розеток и электровыводов
36	План слаботочных сетей
37	План освещения
38	Техническое задание на подбор светильников
39	Управление светильниками
40	План вентиляции
41	План отопления
42	План покрытий пола
43	Раскладка плитки. Планы полов
44	Раскладка плитки. Прихожая. Фартук кухни
45	Развёртка стены А. Спальня 1 (пом. 1)
46	Привязки электроточек, стена А. Спальня 1 (пом. 1)
47	Развёртка стены Б. Спальня 1 (пом. 1)
48	Развёртка стены В. Спальня 1 (пом. 1)
49	Развёртка стены Г. Спальня 1 (пом. 1)
50	Развёртки стен А, Б. Ванная (пом. 2)
51	Развёртки стен В, Г. Ванная (пом. 2)
52	Привязки электроточек и выводов ВК, стены Б, Г. Ванная (пом. 2)
53	Развёртки стен А, Б, В. Гардеробная (пом. 3)
54	Развёртка стены Г. Гардеробная (пом. 3)
55	Развёртка стены А. Спальня 2 (пом. 4)
56	Привязки электроточек, стена А. Спальня 2 (пом. 4)
57	Развёртка стены Б. Спальня 2 (пом. 4)
58	Развёртка стены В. Спальня 2 (пом. 4)
59	Развёртка стены Г. Спальня 2 (пом. 4)
60	Развёртки стен А, В. Прихожая (пом. 5)
61	Развёртка стены Б. Прихожая (пом. 5)
62	Развёртка стены Г. Прихожая (пом. 5)
63	Развёртка стены Б2. Кухня-гостиная (пом. 6), кухонный фронт
64	Развёртка стены В1. Кухня-гостиная (пом. 6), кухонный фронт
65	Привязки электроточек и выводов ВК, стена В1. Кухня-гостиная (пом. 6)
66	Развёртка стены А. Кухня-гостиная (пом. 6)
67	Привязки электроточек, стена А. Кухня-гостиная (пом. 6)
68	Развёртка стены Б1. Кухня-гостиная (пом. 6)
69	Развёртки стен В2, Г1. Кухня-гостиная (пом. 6)
70	Развёртка стены Г2. Кухня-гостиная (пом. 6)
71	Привязки электроточек, стена Г2. Кухня-гостиная (пом. 6)
72	Развёртки стен А, Б, В. Санузел 2 (пом. 7)
73	Привязки электроточек и выводов ВК, стена Б. Санузел 2 (пом. 7)
74	Развёртка стены Г. Санузел 2 (пом. 7)
75	Развёртки стен А, Б. Коридор (пом. 8)
76	Развёртки стен В, Г. Коридор (пом. 8)
77	Открытые вопросы, принятые допущения и конфликты. Лист 1 из 5
78	Открытые вопросы, принятые допущения и конфликты. Лист 2 из 5
79	Открытые вопросы, принятые допущения и конфликты. Лист 3 из 5
80	Открытые вопросы, принятые допущения и конфликты. Лист 4 из 5
81	Открытые вопросы, принятые допущения и конфликты. Лист 5 из 5
Д_1	Шкаф распашной М_05
Д_2	Система хранения М_07
Д_3	Шкаф-купе М_13
Д_4	Кухня (пом. 6). Развёртка гарнитура
С1	Ведомость отделки помещений. Лист 1 из 2
С2	Ведомость отделки помещений. Лист 2 из 2
С3	Спецификация отделочных материалов
С4	Список покупок
С5	Список покупок (окончание)
С6	Узлы. Лист 1 из 2
С7	Узлы. Лист 2 из 2

Общие указания

1. Размеры даны в мм от чистовых поверхностей стен: слой штукатурки 20 мм по блоку и 5 мм шпаклёвки по ГКЛ учтён. Перед заказом встроенной мебели — контрольный обмер после штукатурки.
2. Привязки мебели — от стен и углов помещения, а не от другой мебели.
3. Розетки, выводы и выключатели под мебель — см. лист 35 «План розеток и электровыводов»; сантехприборы и выводы воды — лист 17.
4. План расстановки не является документацией для изготовления мебели: изделия — по чертежам мебельщика; покупную мебель заменять только на изделия не больше габарита из спецификации (лист 13).
5. Встроенная мебель «стена в стену» — с зазором 10 мм с каждой стороны или с компенсаторами.
6. Развёртки — вид на стену изнутри помещения, по часовой стрелке; расположение стен на схеме листа развёртки; размеры — в мм по чистовым поверхностям; отметки — в м от ±0,000; высоты Н — от чистого пола помещения до оси изделия, у декора — до центра.
7. Красная цепочка — привязки электроточек и выводов по осям от угла чистовых стен; высота Н — у знака, от чистого пола до оси; высоты мебели, проёмов и границ отделки колонкой отметок слева. Стена с 5 и более точками или с мелкими звеньями привязок показана двумя видами: архитектурная развёртка (мебель, отделка, проёмы, высоты) и вид «Привязки» на отдельном листе — точки и выводы с марками, одна цепочка по осям и таблица привязок (каждая точка — строка).
8. У знака электроточки: марка (Р — розетка, S — выключатель, Св — светильник, ЭВ вывод кабеля), ×N — число постов в рамке, гр. — группа щита, Н — высота оси от чистого пола, мм; группы по клавишам выключателя — на листе выключателей.
9. Схема мебели, приборов и декора не является технической документацией для производства мебели; габариты — по паспортам изделий.
10. Марки позиций: М_NN — мебель, ОБ_NN — оборудование, С_NN — сантехника; О-N отделка (ведомость отделочных материалов, серия С).
11. Размеры мебели и изделий на заказ уточнить по месту после отделочных работ.

					Проект: Трёхкомнатная квартира
	Лист	№ док.	Подпись	Дата	
Дизайнер	Кырлан А.С.			04.11.26	Список листов
					Стадия: П; Лист: 3; Листов: 92

выпуск 04.11.2026 № 503a52061a · стр. 3 из 92

Что в альбоме

Альбом — дизайн-проект с рабочими чертежами для ремонта. Листы идут в порядке работ: титул и вводные, реестр открытых вопросов и решений, планы (обмер, монтаж стен, мебель, двери, потолки, полы), инженерия (сантехника, электрика, вентиляция и отопление), развёртки стен с визуализациями помещений, чертежи мебели, ведомости материалов и узлы.

Вам как заказчику — титул, эта вводная, «Ваш проект на одной странице», реестр вопросов, план мебели, визуализации и развёртки, ведомости мебели и материалов. Подрядчику — всё остальное: монтажные планы, привязки выводов и розеток, узлы, ведомости объёмов.

Знаки на листах

Без знака — решение утверждено или подтверждено обмером.

Что проверить до ремонта

1. Розетки у кровати и рабочего места: хватает ли их с каждой стороны кровати и над столом (план розеток — лист 35).

2. Выводы под технику — варочная панель, духовка, посудомойка, стиральная машина, бойлер: совпадают ли с выбранными моделями (листы 13, 14, 15, 35).

3. Высоты розеток, выключателей и выводов даны от чистого пола: если мебель или техника будут другими — скажите до штробления стен.

Номера записей

К-N — открытый вопрос: чего не хватает или что выбрать (варианты и рекомендация — в тексте). Пока ответа нет, действует строка «если решения нет».

Кф-N — конфликт между разделами (например, мебель и радиатор в одном месте); закрывается решением, которое записывается как ИЗ-N.

ИЗ-N — изменение проекта: что было, что стало и кто утвердил. Изменение без подписи предложение.

Все записи — на листе реестра сразу после вводных; на других листах на них стоят ссылки.

Почему альбом предварительный

Обмера на объекте не было: размеры взяты с плана заказчика. Технические условия (мощность, вода, вентиляция дома) не получены, часть решений ждёт вашего ответа. Пока в реестре есть открытые вопросы, альбом предварительный — пометка в штампе снимается закрытием вопросов, а не стиранием.


Правку к любому листу можно оставить по кнопке «Правка к листу» или на сайте студии: дизайн-студия-квартир.рф — укажите номер листа и что изменить.

3 круга правок входят в цену; условия — в договоре и на странице вашего заказа на сайте студии.

					Проект: Трёхкомнатная квартира
	Лист	№ док.	Подпись	Дата	Как читать альбом
Дизайнер	Кырлан А.С.			04.11.26	

Стадия	Лист	Листов
П	4	92

выпуск 04.11.2026 № 503a52061a · стр. 4 из 92

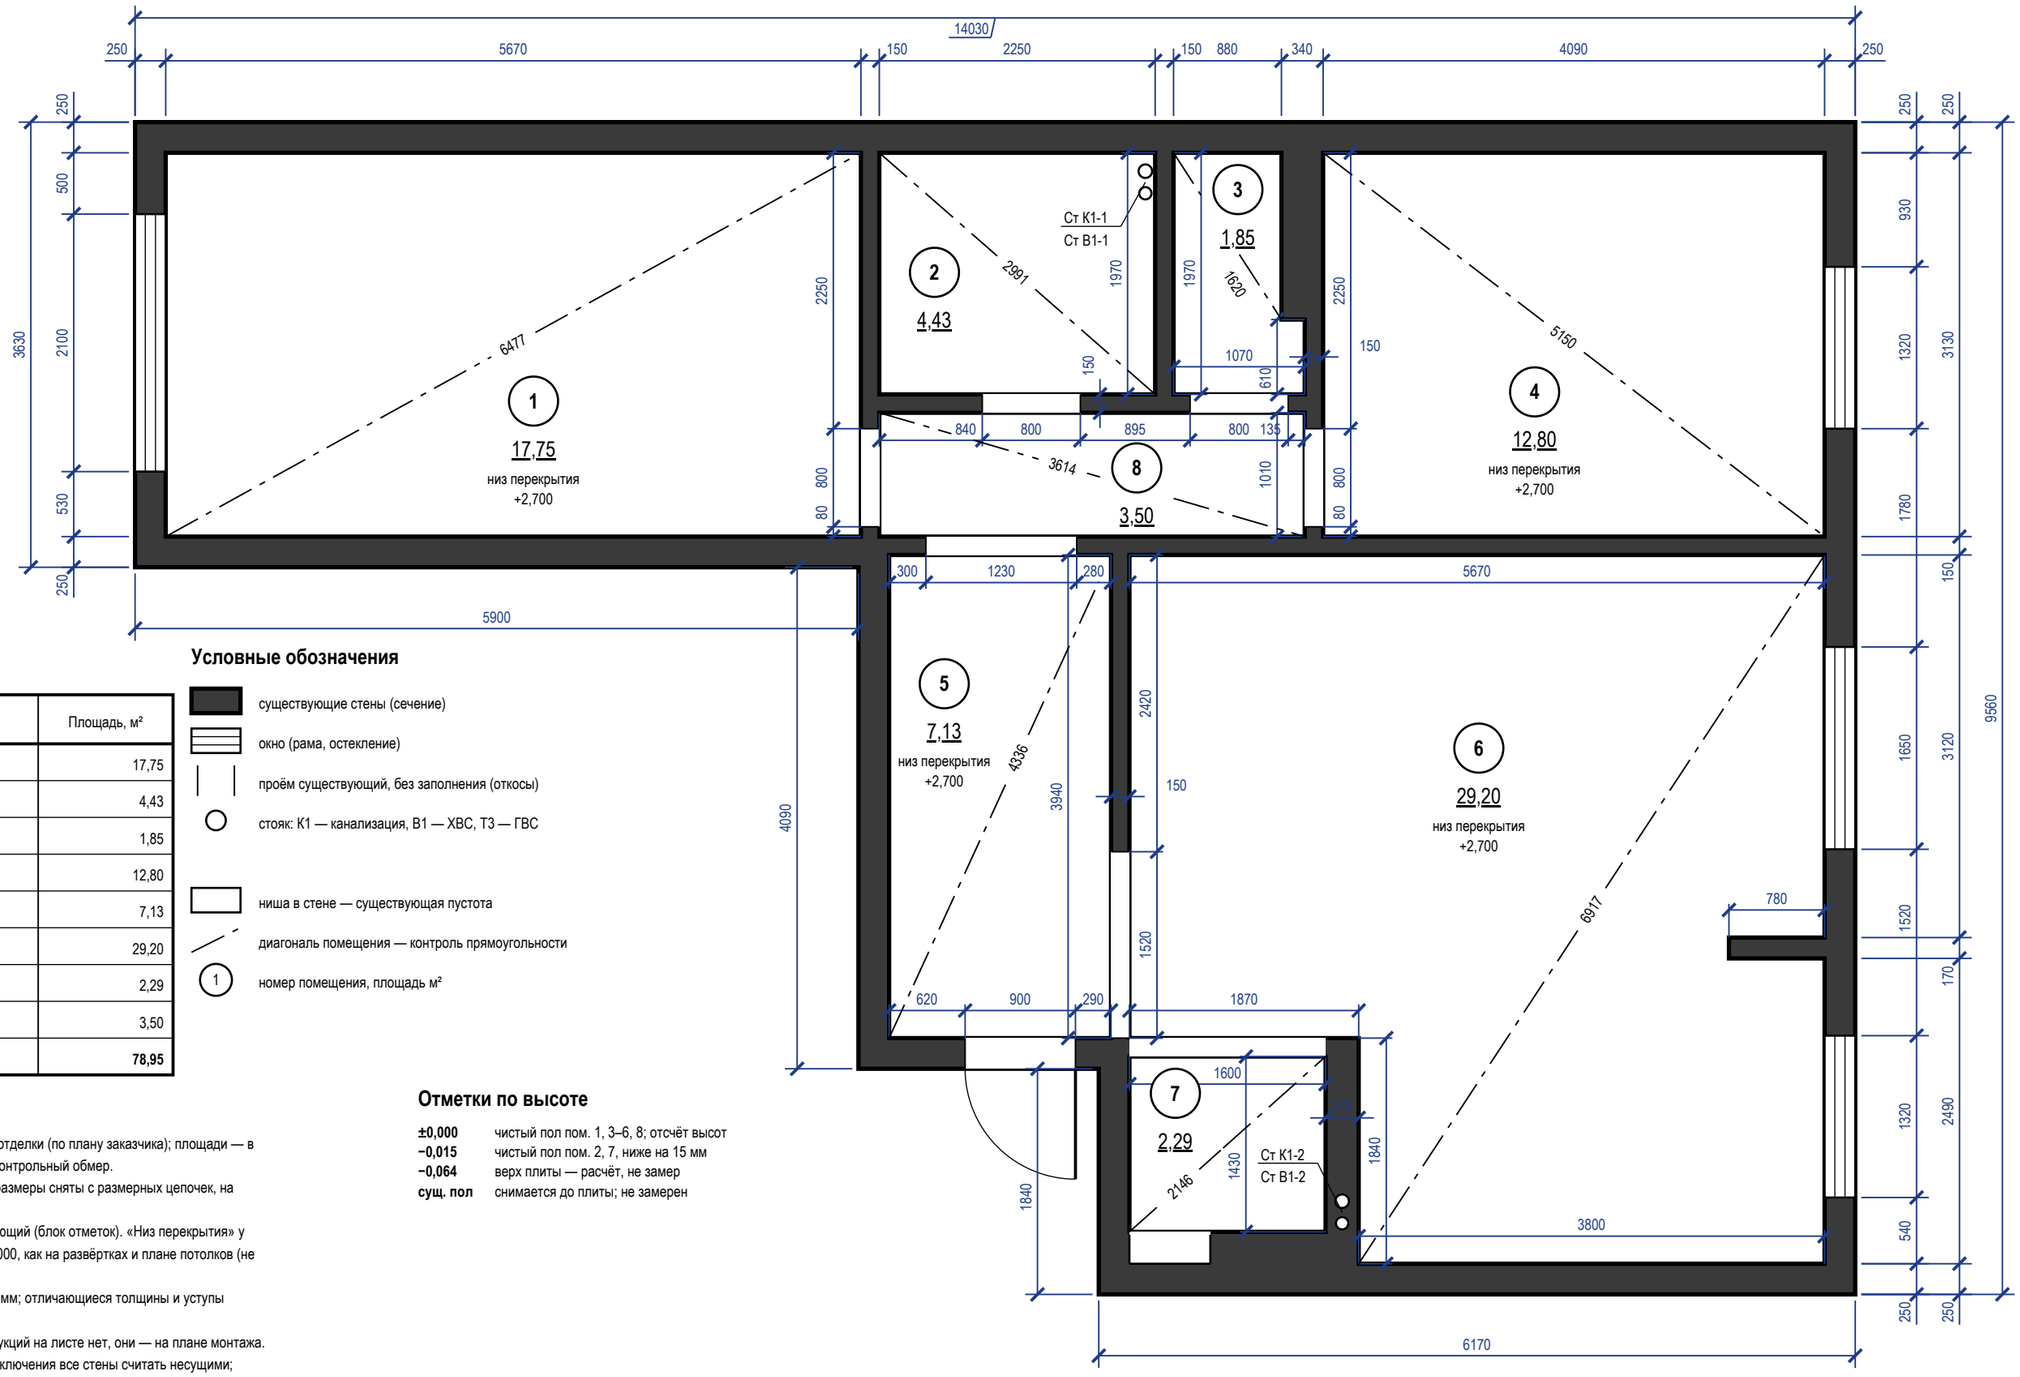

Экспликация помещений

№	Наименование	Площадь, м²
1	Спальня 1	17,75
2	Ванная	4,43
3	Гардеробная	1,85
4	Спальня 2	12,80
5	Прихожая	7,13
6	Кухня-гостиная	29,20
7	Санузел 2	2,29
8	Коридор	3,50
	Итого (общая площадь)	**78,95**

Условные обозначения

- существующие стены (сечение)
- окно (рама, остекление)
- проём существующий, без заполнения (откосы)
- стояк: К1 — канализация, В1 — ХВС, Т3 — ГВС
- ниша в стене — существующая пустота
- диагональ помещения — контроль прямоугольности
- (1) номер помещения, площадь м²

Примечания


1. Размеры — в мм по чистым поверхностям стен до отделки (по плану заказчика); площади — в м² по тем же размерам. До начала работ выполнить контрольный обмер.
2. Источник плана: растровый скан плана заказчика, размеры сняты с размерных цепочек, на объекте не замерены.
3. За отметку ±0,000 принят чистый пол, не существующий (блок отметок). «Низ перекрытия» у марки помещения — отметка низа перекрытия от ±0,000, как на развёртках и плане потолков (не высота потолка: потолок — по плану потолков).
4. Толщины стен: наружные 250 мм, перегородки 150 мм; отличающиеся толщины и уступы размерами на плане.
5. Обмер — существующее положение: новых конструкций на листе нет, они — на плане монтажа.
6. Несущие стены не определены: до технического заключения все стены считать несущими; проёмы и штробы в них не выполнять.
7. Дверные проёмы показаны без заполнения (двери — лист 29); высота дверных проёмов 2100 мм, проёмов без двери 2500, 2100 мм; низ окон (подоконник) 900 мм от чистого пола, высота окон 1500, 1400 мм.
8. Диагонали — контрольные размеры; расхождение более 5 мм подписать на плане как перекос.
9. Размеры проверить на месте до начала работ; расхождение контрольных промеров ≤ 2 %.

Отметки по высоте

±0,000	чистый пол пом. 1, 3–6, 8; отсчёт высот
−0,015	чистый пол пом. 2, 7, ниже на 15 мм
−0,064	верх плиты — расчёт, не замер
сущ. пол	снимается до плиты; не замерен

					Проект: Трёхкомнатная квартира	**М 1:50**
	Лист	№ док.	Подпись	Дата		
Дизайнер	Кырлан А.С.			04.11.26	План планировки от заказчика	Стадия: П; Лист: 5; Листов: 92

выпуск 04.11.2026 № 503a52061a · стр. 5 из 92

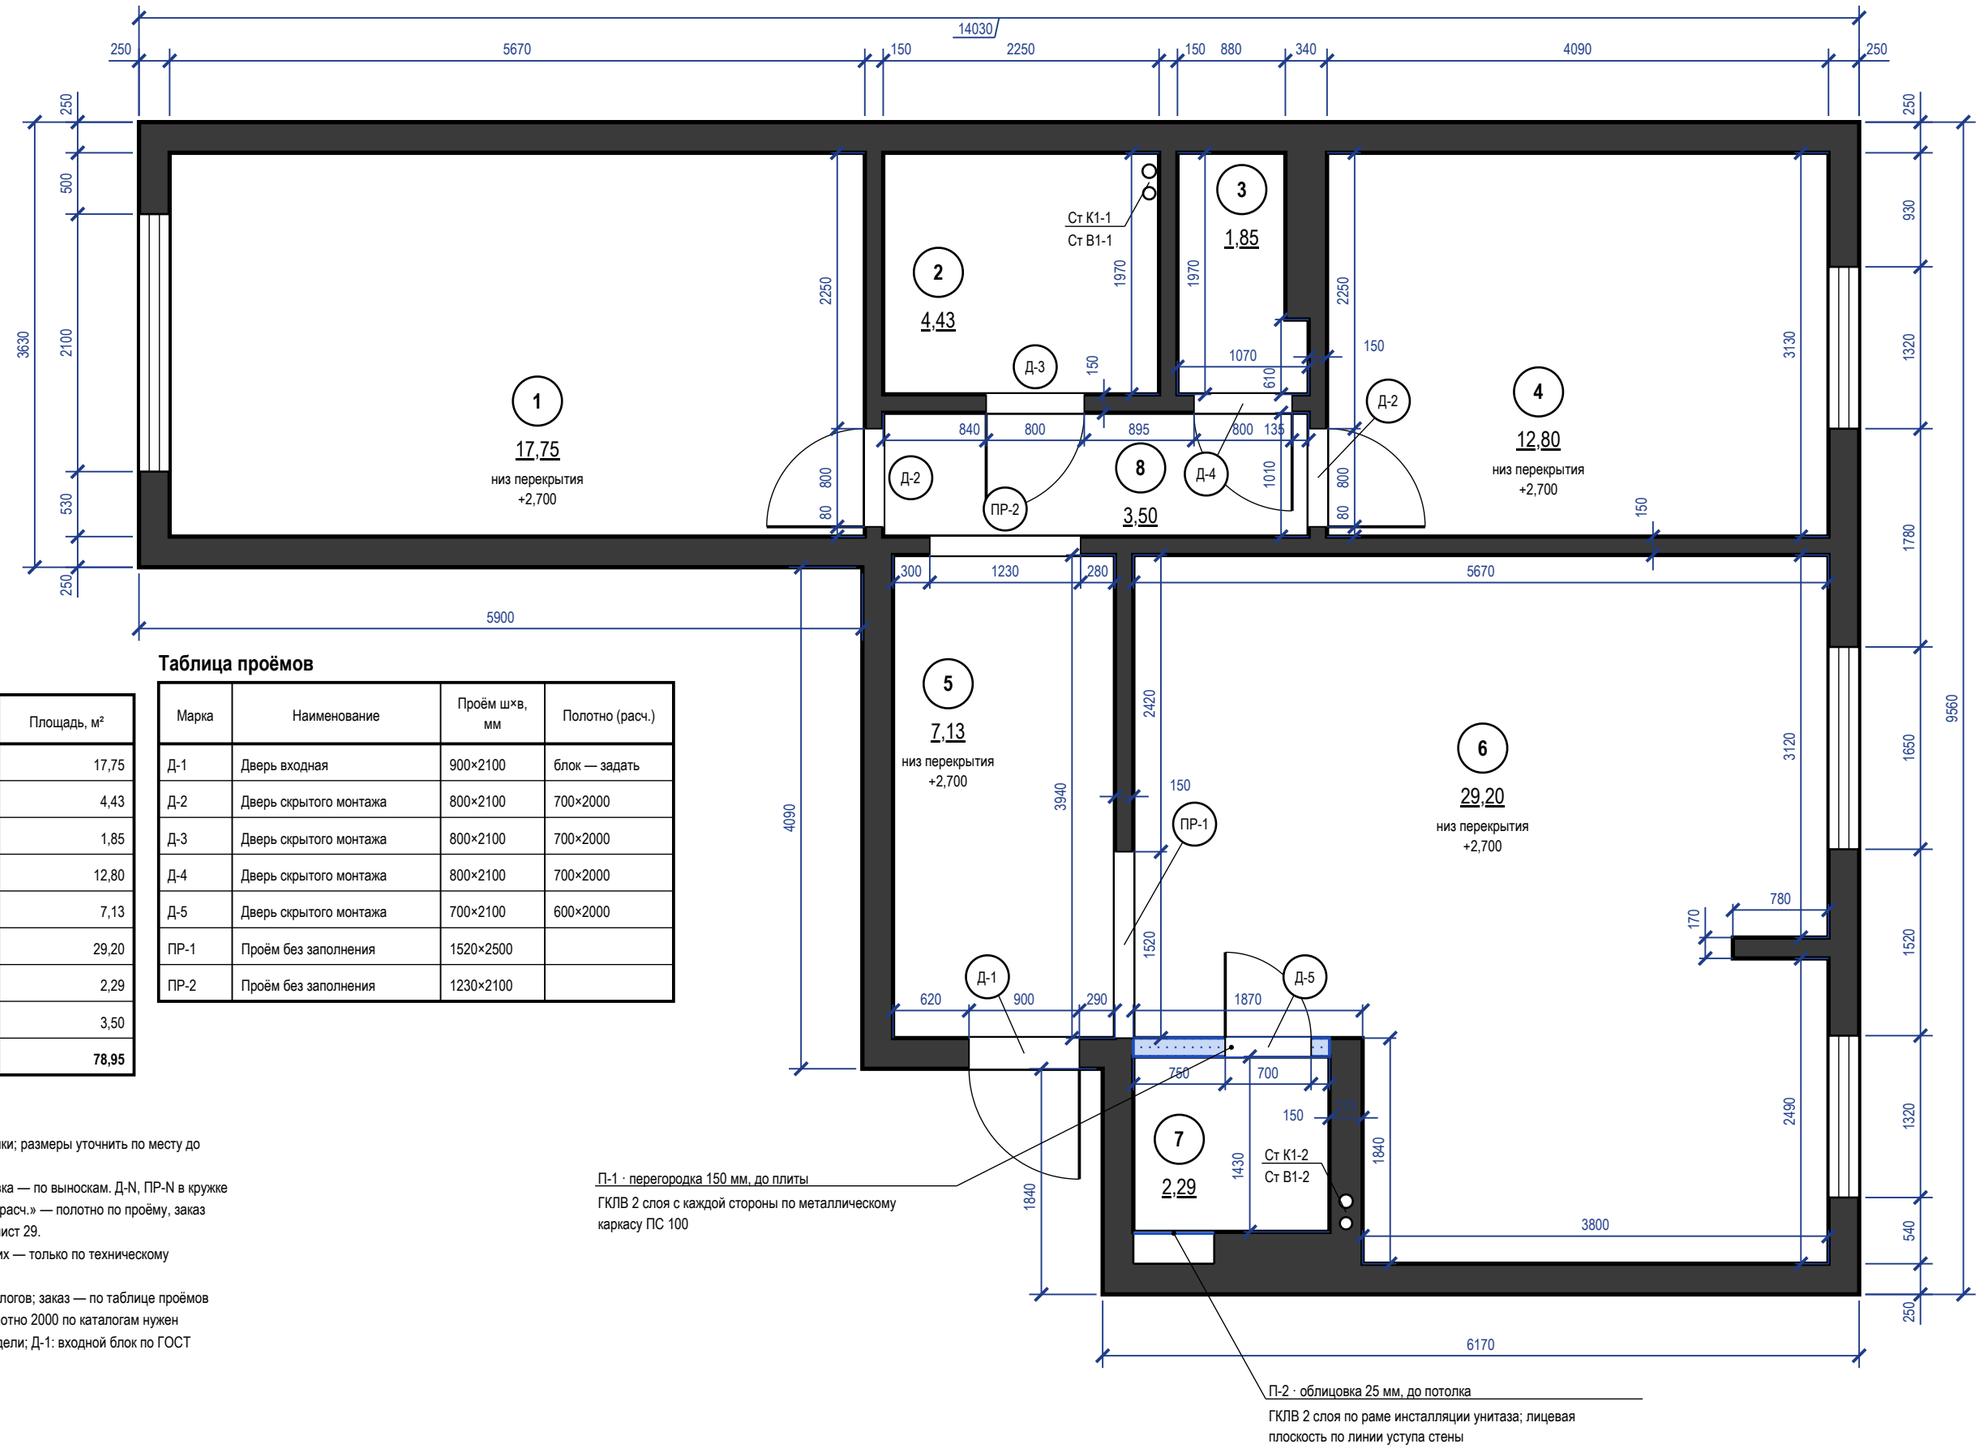

П-1 · перегородка 150 мм, до плиты
ГКЛВ 2 слоя с каждой стороны по металлическому каркасу ПС 100

П-2 · облицовка 25 мм, до потолка
ГКЛВ 2 слоя по раме инсталляции унитаза; лицевая плоскость по линии уступа стены

Экспликация помещений

№	Наименование	Площадь, м²
1	Спальня 1	17,75
2	Ванная	4,43
3	Гардеробная	1,85
4	Спальня 2	12,80
5	Прихожая	7,13
6	Кухня-гостиная	29,20
7	Санузел 2	2,29
8	Коридор	3,50
	Итого (общая площадь)	**78,95**

Таблица проёмов

Марка	Наименование	Проём ш×в, мм	Полотно (расч.)
Д-1	Дверь входная	900×2100	блок — задать
Д-2	Дверь скрытого монтажа	800×2100	700×2000
Д-3	Дверь скрытого монтажа	800×2100	700×2000
Д-4	Дверь скрытого монтажа	800×2100	700×2000
Д-5	Дверь скрытого монтажа	700×2100	600×2000
ПР-1	Проём без заполнения	1520×2500	
ПР-2	Проём без заполнения	1230×2100	


Примечания

1. Размеры — в мм от чистовых поверхностей стен до отделки; размеры уточнить по месту до начала работ.
2. Новые перегородки и облицовки — синим; каркас и обшивка — по выноскам. Д-N, ПР-N в кружке — марка проёма: проём и полотно — по таблице проёмов, «расч.» — полотно по проёму, заказ по выбранной модели; ведомость, отделка и фурнитура — лист 29.
3. Несущие стены не изменять: проёмы, ниши и штробы в них — только по техническому заключению.
4. «расч.» — полотно, выведенное из проёма по запасу каталогов; заказ — по таблице проёмов выбранной модели; Д-2, Д-3, Д-4, Д-5: проём 2100, а под полотно 2000 по каталогам нужен 2050–2080, под 2100 — 2150–2180: высоту проёма — по модели; Д-1: входной блок по ГОСТ 31173-2016 — задать при выборе блока.

					Проект: Трёхкомнатная квартира	**М 1:50**
	Лист	№ док.	Подпись	Дата		
Дизайнер	Кырлан А.С.			04.11.26	План монтажный	Стадия: П; Лист: 6; Листов: 92

выпуск 04.11.2026 № 503a52061a · стр. 6 из 92


Вид на каркас без обшивки (М 1:20)

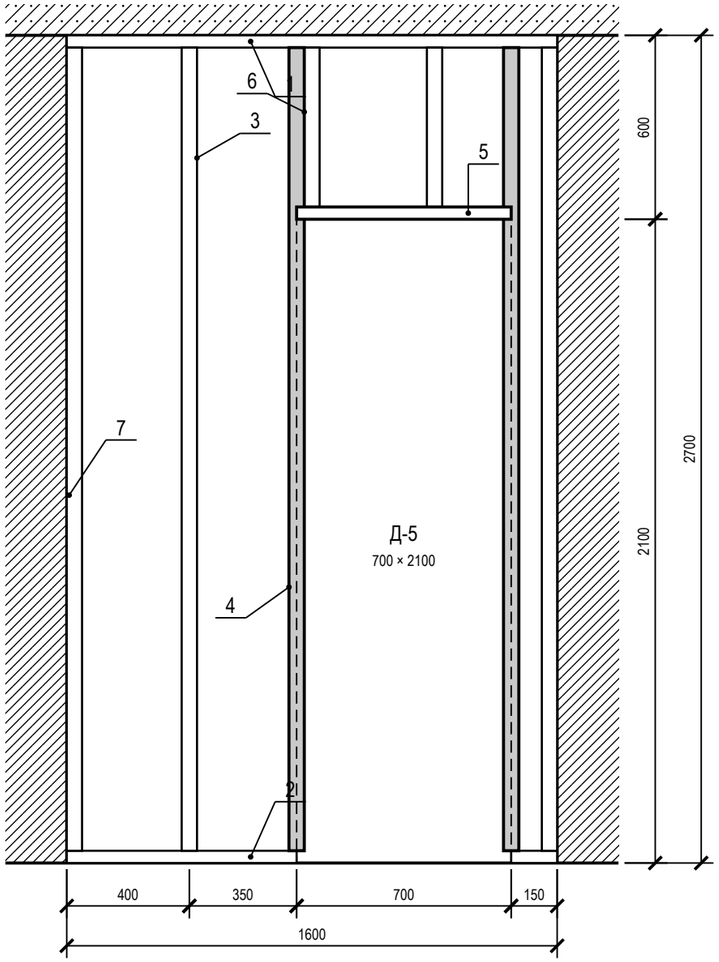

Оси — стойки каркаса; полки профиля на виде условны

Сечение А–А по стойке (М 1:5)


сверху — пом. 6, окраска

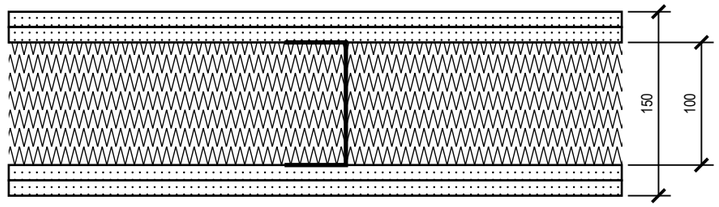

снизу — пом. 7, плитка


поз. 9 — ГКЛВ 12,5 мм в 2 слоя с каждой стороны; поз. 3 — ПС 100; поз. 8 — минвата 100 мм (принято)

Сечение Б–Б у проёма, на уровне ниже перемычки (М 1:5)

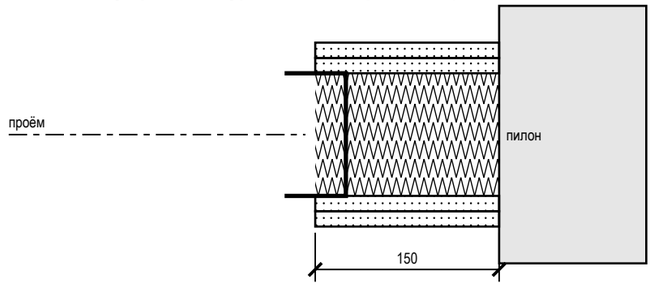


поз. 4 — УА 100, обрамление проёма; обшивка по краю проёма, простенок 150 мм до пилона

Узел 1. К плите (М 1:5)

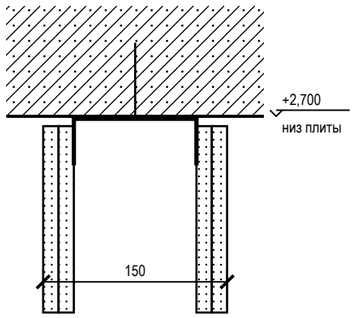

Узел 2. К полу (М 1:5)

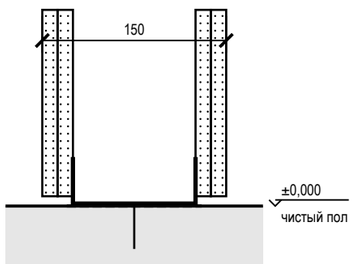

Ведомость элементов каркаса

Поз.	Наименование	Кол-во	Ед.
1	ПН 100 по потолку (к перекрытию)	1,60	м
2	ПН 100 по полу, без проёма	0,90	м
3	ПС 100 через 400 мм	3 × 2,70	м
4	УА 100 по краям проёма	2 × 2,70	м
5	ПН 100 перемычка над проёмом	0,70	м
6	ПС 100 над перемычкой	2 × 0,60	м
7	Лента уплотнительная под профили	7,90	м
8	Минвата в полость, 100 мм	2,85	м²
9	ГКЛВ 12,5 мм, 2 слоя с двух сторон	11,40	м²

Итого: ПН 3,20 м, ПС 9,30 м, УА 5,40 м; сторона 2,85 м²

Примечания


1. П-1 (С112, ГКЛВ в 2 слоя с каждой стороны, толщина 150 мм, высота 2700 мм до плиты); ось и длина 1600 мм — со скана плана заказчика (контрольный обмер не выполнялся).
2. Шаг стоек 400 мм — по данным (под плитку и во влажной зоне). Размеры сечений профилей — «ПС 100», «УА 100» по данным и каталогу; толщины листов — ГОСТ 32614-2012.
3. Проём Д-5 в каркасе 700 × 2100 мм принят по размеру полотна: короб скрытой двери (модель, размеры) не выбран — проём пересчитать по коробке до монтажа УА.
4. Перемычка над проёмом — направляющий профиль по верху проёма на всю его ширину; короткие стойки ПС над перемычкой на шаге каркаса: по практике узла Knauf, не по данным объекта.
5. Заполнение полости — минераловатная плита на всю глубину профиля (Rw системы С112 нормируют с заполнением); марка и плотность выбираются при закупке.
6. Длина стойки равна высоте перегородки: стойки режут на высоту между направляющими при монтаже, зазоры до плиты и пола в проекте не заданы.
7. Обшивку крепят к стойкам шурупами через слой, швы слоёв вразбежку; зазоры обшивки до плиты и пола, шаг дюбелей, марка заполнения — по ТУ системы и узлу изготовителя.

					Проект: Трёхкомнатная квартира — **по видам**
	Лист	№ док.	Подпись	Дата	
Дизайнер	Кырлан А.С.			04.11.26	Схема каркаса перегородки П-1


Стадия	Лист	Листов
П	7	92

выпуск 04.11.2026 № 503a52061a · стр. 7 из 92

Привязка выводов и крепление модулей

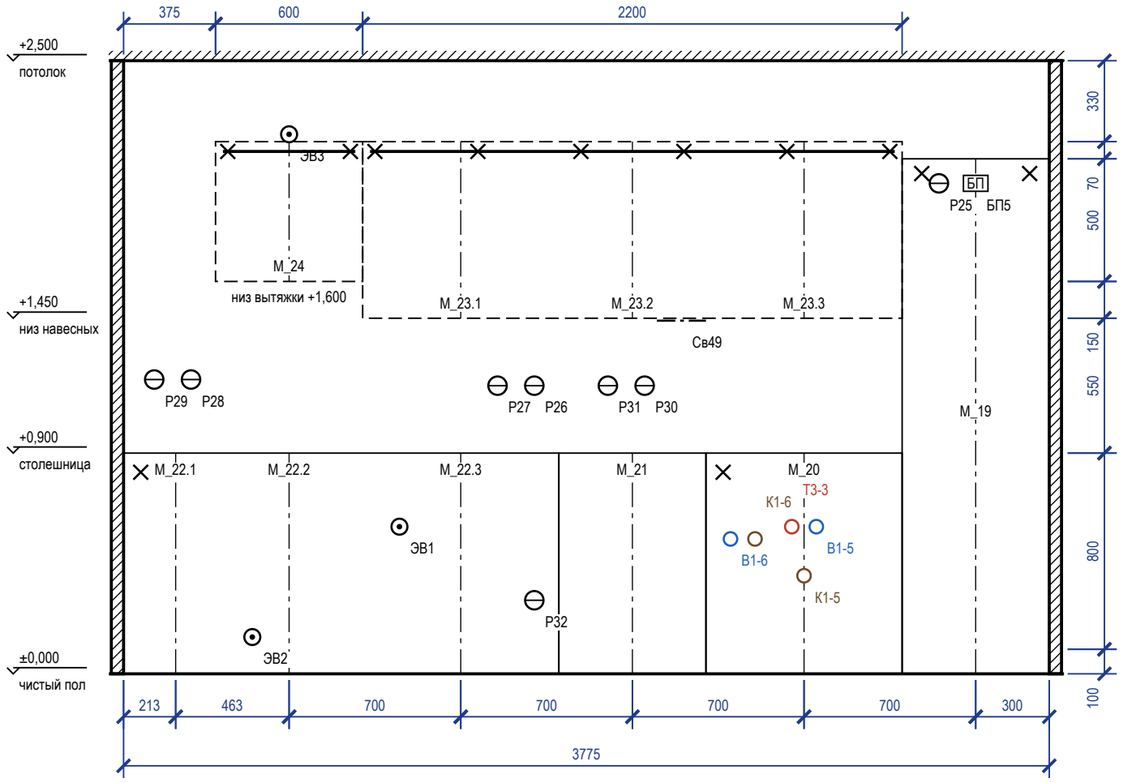

План столешницы

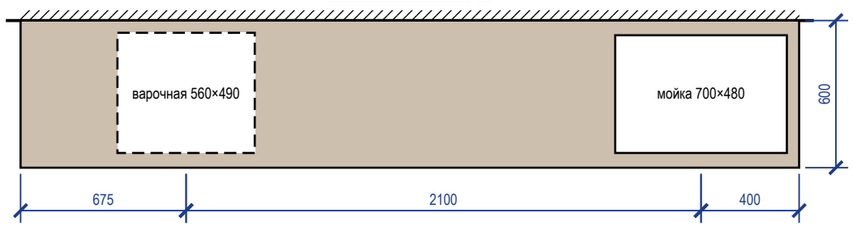

Примечания

1. Выводы — по проекту электрики и ВК; привязка по горизонтали — от оси модуля (плюс — вправо по виду), по высоте — от чистого пола до оси вывода.
2. Пенал — уголки к стене 2 шт. сверху; нижние модули — стяжками между собой и уголком к стене; ряд выставить по уровню опорами цоколя.
3. Розетки над столешницей — не ниже 150 мм над ней и не за корпусом техники; розетка за ПММ, духовым шкафом и холодильником — только в соседнем модуле или в зоне цоколя с доступом.
4. Столешница — вырезы по шаблонам выбранных моделей мойки и варочной панели; торцы у стены — герметик, пристеночный плинтус.

Привязка выводов к осям модулей

Код	Назначение	Модуль	От оси, мм	Н, мм	Размещение
Р29	розетка — фартук	M_22.1	−87	1200	над столешницей (фартук)
Р28	розетка ×2 — фартук	M_22.1	+63	1200	над столешницей (фартук)
ЭВ2	вывод кабеля — духовой шкаф	M_22.2	−150	150	под духовым шкафом, доступ через ящик
ЭВ3	вывод кабеля — вытяжка — над корпусом	M_24	0	2200	в навесном модуле
ЭВ1	вывод кабеля — варочная панель — за ящиком	M_22.3	−250	600	в соседнем модуле, за ящиком
Р27	розетка — фартук	M_22.3	+150	1175	над столешницей (фартук)
Р26	розетка ×2 — фартук	M_22.3	+300	1175	над столешницей (фартук)
Р32	розетка — посудомоечная машина	M_22.3	+300	300	в соседнем модуле, за ящиком
Р31	розетка — фартук между мойкой и варочной	M_21	−100	1175	над столешницей (фартук)
Р30	розетка ×2 — фартук между мойкой и варочной	M_21	+50	1175	над столешницей (фартук)
Св49	светодиодная лента — подсветка столешницы	M_21	+200	1440	в профиле по низу навесного модуля
В1-6	В1 — кран ПММ в шкафу мойки	M_20	−300	550	в модуле мойки
К1-6	К1 Ø40 — слив ПММ в шкафу мойки	M_20	−200	550	в модуле мойки
Т3-3	Т3 — межос. 100	M_20	−50	600	в модуле мойки
К1-5	К1 Ø50 — мойка	M_20	0	400	в модуле мойки
В1-5	В1 — межос. 100	M_20	+50	600	в модуле мойки
Р25	розетка — холодильник — в своём модуле, над нишей, за съёмной панелью	M_19	−150	2000	над нишей холодильника, съёмная панель
БП5	блок питания — в пенале M_19, верх, съёмная панель	M_19	0	2000	над нишей холодильника, съёмная панель

Зазоры под отделку


Поверхность	Отделка	Зазор, мм	Учесть
фартук	керамогранит	10	от чернового основания до корпуса навесных и столешницы
стены	окраска	5	под штукатурку и шпаклёвку за пеналом
пол	инженерная доска		цоколь — после укладки пола, опоры ±20 мм

Условные обозначения


- нижний модуль, пенал (контур)
- невидимый контур: навесной модуль, корпус под столешницей
- ось модуля (от неё — привязка вывода)
- анкер / уголок крепления к стене
- розетка на стене
- вывод кабеля к технике
- В1 — вывод воды В1 / Т3, канализации К1

					Проект: Трёхкомнатная квартира — М 1:25
	Лист	№ док.	Подпись	Дата	
Дизайнер	Кырлан А.С.			04.11.26	Кухня (пом. 6). Монтажная схема
					Стадия: П; Лист: 8; Листов: 92


Шкаф распашной M_05 (пом. 1)

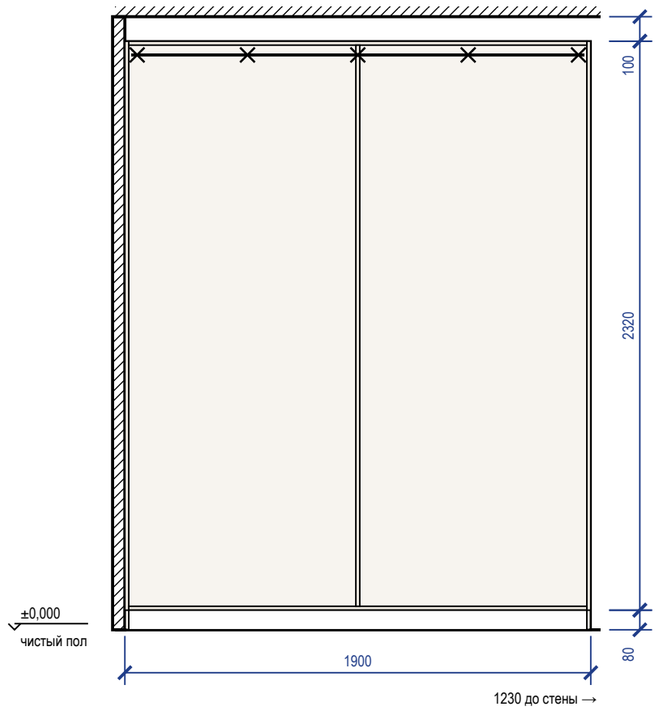

Система хранения M_07 (пом. 3)

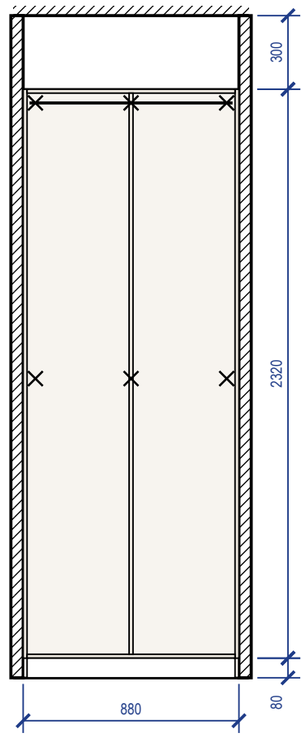

Шкаф-купе M_13 (пом. 5)

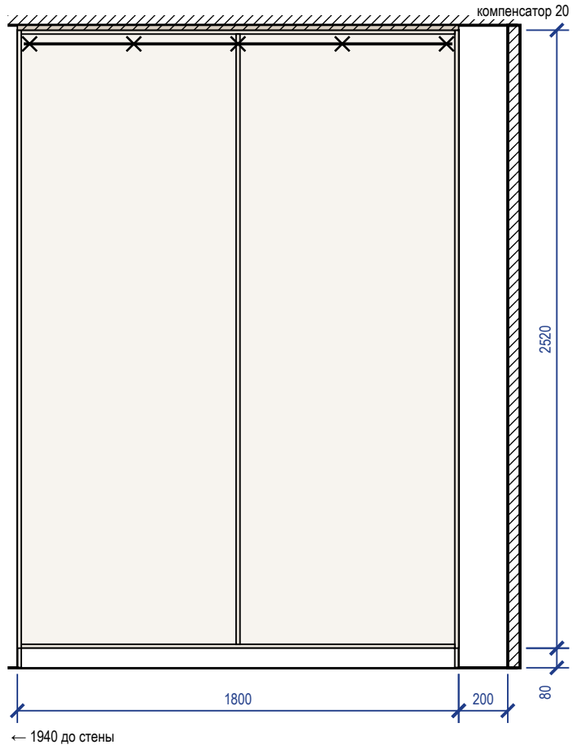

Крепление и зазоры под отделку

Марка	Помещение, стена	Основание	Отделка стены	Зазор, мм	Крепёж по планке	От опрокидывания
M_05	Спальня 1 (1), стена Б	по основанию — см. таблицу крепежа	окраска	5	анкер 5 шт., шаг 450	уголок к стене, 2 шт.
M_07	Гардеробная (3), стена А	по основанию — см. таблицу крепежа	окраска	5	анкер 6 шт. (2 ряда)	крепление к стене, 3 точки
M_13	Прихожая (5), стена Г	по основанию — см. таблицу крепежа	окраска	5	анкер 5 шт., шаг 425	уголки 2 шт.

Крепёж по основанию стены

Основание стены	Крепёж
бетон, ж/б	анкер-шуруп 7,5×72 или дюбель 8×60 с шурупом 5×70
кирпич полнотелый	дюбель 8×80 с шурупом 5×90
газобетон, пазогребень	дюбель для газобетона 10×100 или химический анкер
гипсокартон	закладная до обшивки (брус 40×80 или фанера 18 мм), саморез в закладную


Условные обозначения

- анкер / уголок крепления к стене
- корпус и полки ЛДСП (вид на стену)
- компенсатор — короб до потолка

Примечания

1. Установочные размеры — от чистого пола и чистых стен; перед установкой контрольный замер после отделки.
2. Порядок: корпус выставить по уровню опорами цоколя → закрепить к стене по задней планке → навесить двери и фасады, отрегулировать зазоры → подогнать и закрепить компенсатор.
3. Анкеры — с шагом не более 500 мм, не ближе 50 мм от края планки; на ГКЛ только в закладную, установленную до обшивки.
4. Скрытые коммуникации под анкеры проверить детектором; трассы электрики по плану розеток.
5. Сборка стоя на месте: M_13 — корпус не собирается лёжа и не поднимается собранным, а собирается в проектном положении у стены; выставление по уровню и крепление к стене выполняются по корпусу, собранному на месте.

					Проект: Трёхкомнатная квартира	M 1:25
	Лист	№ док.	Подпись	Дата		
Дизайнер	Кырлан А.С.			04.11.26	Шкафы. Монтажная схема	Стадия: П; Лист: 9; Листов: 92

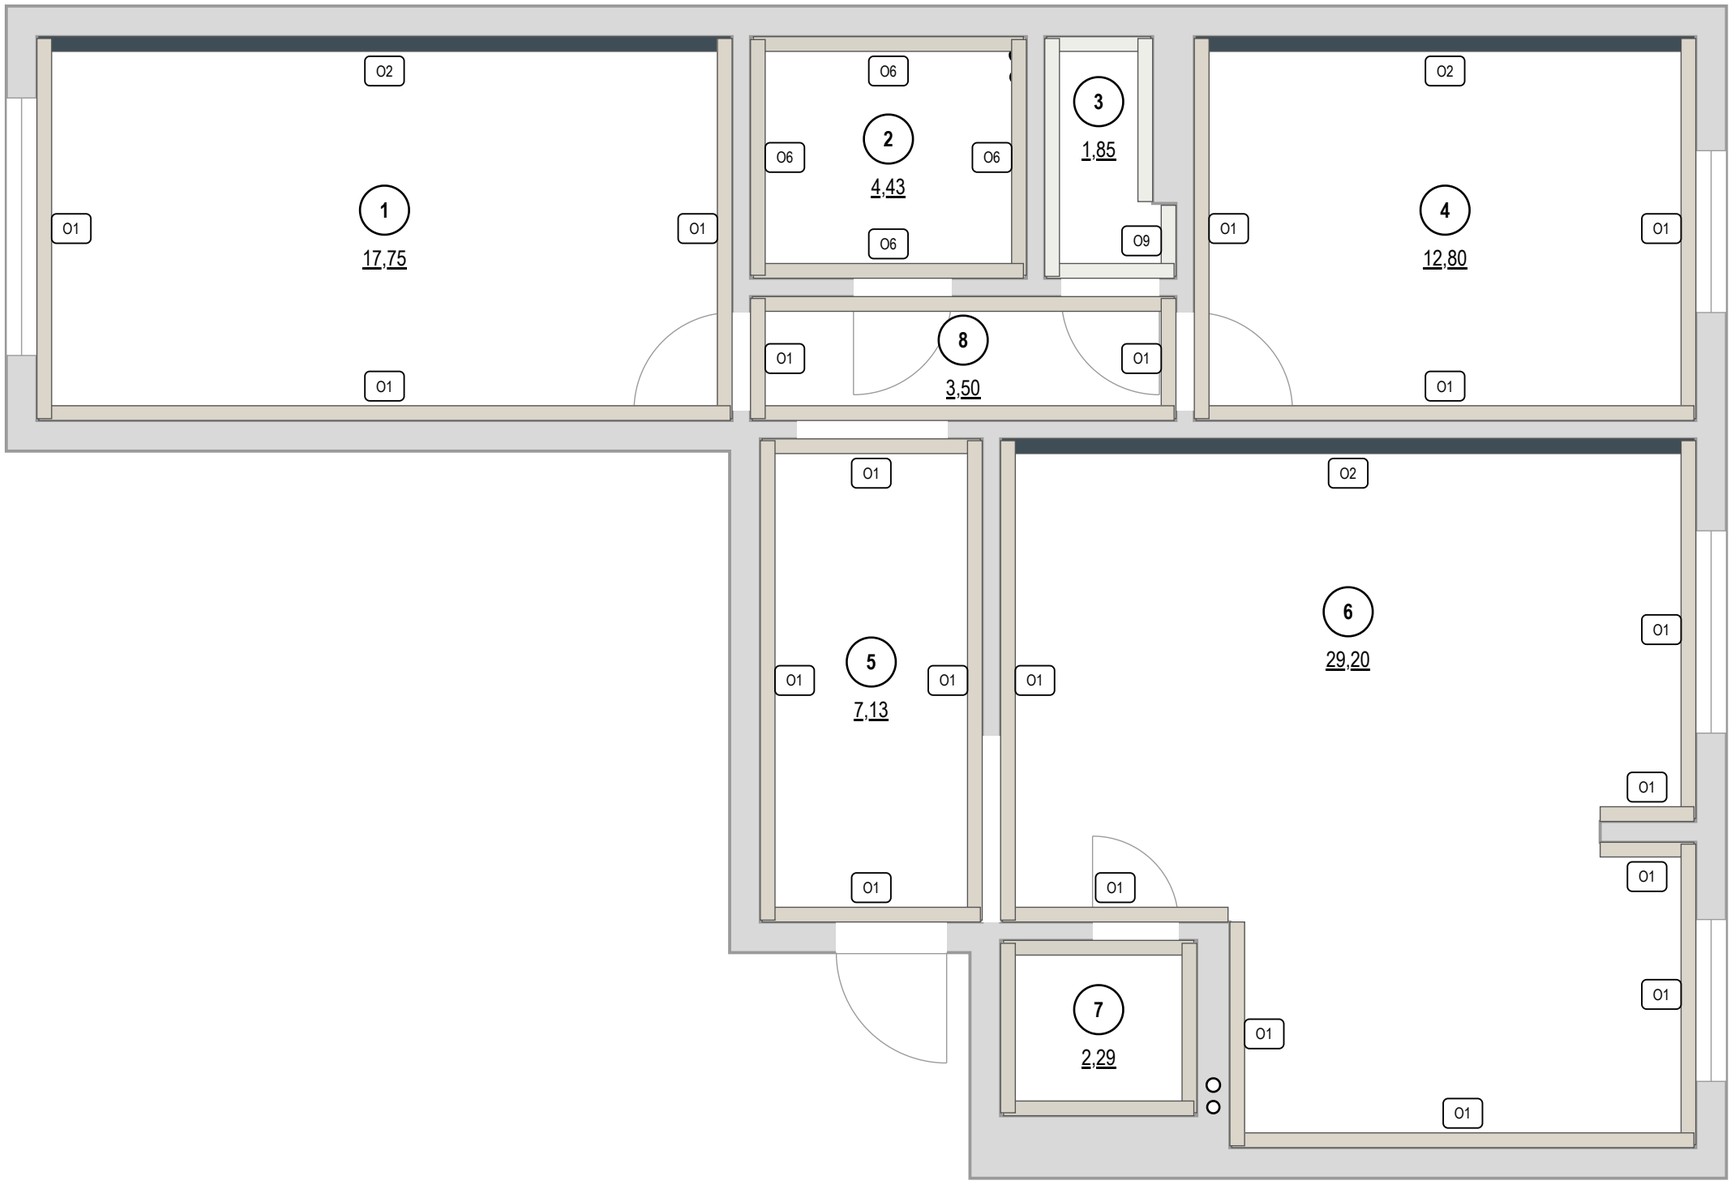

Покрытия стен

Марка	Покрытие	Помещение: S, м²	Итого, м²
O1	окраска Farrow & Ball · No. 241 «Skimming Stone»	1: 25,1; 4: 22,4; 5: 21,6; 6: 35,4; 8: 13,9	118,3
O2	окраска Farrow & Ball · No. 30 «Hague Blue»	1: 14,1; 4: 10,2; 6: 14,1	38,4
O6	облицовка плиткой · 600×1200 мм	2: 18,1; 7: 12,6	30,8
O9	окраска Tikkurila · V503 «Winter»	3: 13,8	13,8

Площади — нетто, по развёрткам (за вычетом проёмов и фартука); высоты помещений — от чистого пола.

					Проект: Трёхкомнатная квартира	**М 1:50**
	Лист	№ док.	Подпись	Дата		
Дизайнер	Кырлан А.С.			04.11.26	Карта покрытий стен	Стадия: П; Лист: 10; Листов: 92

Колерная карта по помещениям

Помещение	Поверхность	Образец	Поз.	Система и код цвета	Производитель, линейка / материал, артикул	Блеск	Класс истирания	LRV	Площадь
1. Спальня 1 17,75 м²	стены		**К1**	Farrow & Ball No. 241	Farrow & Ball · Modern Emulsion	матовая	1	67	25,0 м²
	акцент А		**К2**	Farrow & Ball No. 30	Farrow & Ball · Modern Emulsion	матовая	1	7	14,2 м²
	потолок		**К3**	Tikkurila V503	Tikkurila · Anti-Reflex 2	глубокомат.	2	86	17,8 м²
	пол		**КМ1**	по образцу	инженерная доска · аналог по хар.				17,8 м²
	плинтус		**К4**	Farrow & Ball No. 241	МДФ · в цвет Farrow & Ball			67	16,8 м
2. Ванная 4,43 м²	стены		**КМ2**	по образцу	плитка · аналог по хар.				18,6 м²
	потолок		**К5**	Tikkurila V503	Tikkurila · Luja 7	матовая	1	86	4,4 м²
	пол		**КМ3**	по образцу	керамогранит · аналог по хар.				4,4 м²
3. Гардеробная 1,85 м²	стены		**К6**	Tikkurila V503	Tikkurila · Harmony	матовая	1	86	14,7 м²
	потолок		**К3**	Tikkurila V503	Tikkurila · Anti-Reflex 2	глубокомат.	2	86	1,9 м²
	пол		**КМ1**	по образцу	инженерная доска · аналог по хар.				1,9 м²
	плинтус		**К7**	Tikkurila V503	МДФ · в цвет Tikkurila			86	5,3 м
4. Спальня 2 12,8 м²	стены		**К1**	Farrow & Ball No. 241	Farrow & Ball · Modern Emulsion	матовая	1	67	22,2 м²
	акцент А		**К2**	Farrow & Ball No. 30	Farrow & Ball · Modern Emulsion	матовая	1	7	10,2 м²
	потолок		**К3**	Tikkurila V503	Tikkurila · Anti-Reflex 2	глубокомат.	2	86	12,8 м²
	пол		**КМ1**	по образцу	инженерная доска · аналог по хар.				12,8 м²
	плинтус		**К4**	Farrow & Ball No. 241	МДФ · в цвет Farrow & Ball			67	13,6 м
5. Прихожая 7,13 м²	стены		**К1**	Farrow & Ball No. 241	Farrow & Ball · Modern Emulsion	матовая	1	67	21,9 м²
	потолок		**К3**	Tikkurila V503	Tikkurila · Anti-Reflex 2	глубокомат.	2	86	7,1 м²
	пол		**КМ4**	по образцу	керамогранит · аналог по хар.				7,1 м²
	плинтус		**К4**	Farrow & Ball No. 241	МДФ · в цвет Farrow & Ball			67	7,8 м
6. Кухня-гостиная 29,2 м²	стены		**К1**	Farrow & Ball No. 241	Farrow & Ball · Modern Emulsion	матовая	1	67	35,5 м²
	акцент А		**К2**	Farrow & Ball No. 30	Farrow & Ball · Modern Emulsion	матовая	1	7	14,2 м²
	потолок		**К3**	Tikkurila V503	Tikkurila · Anti-Reflex 2	глубокомат.	2	86	29,2 м²
	пол		**КМ1**	по образцу	инженерная доска · аналог по хар.				29,2 м²
	плинтус		**К4**	Farrow & Ball No. 241	МДФ · в цвет Farrow & Ball			67	22,2 м
	фартук		**КМ5**	по образцу	керамогранит · аналог по хар.				1,9 м²
7. Санузел 2 2,29 м²	стены		**КМ2**	по образцу	плитка · аналог по хар.				13,1 м²
	потолок		**К5**	Tikkurila V503	Tikkurila · Luja 7	матовая	1	86	2,3 м²
	пол		**КМ3**	по образцу	керамогранит · аналог по хар.				2,3 м²
8. Коридор 3,5 м²	стены		**К1**	Farrow & Ball No. 241	Farrow & Ball · Modern Emulsion	матовая	1	67	14,2 м²
	потолок		**К3**	Tikkurila V503	Tikkurila · Anti-Reflex 2	глубокомат.	2	86	3,5 м²
	пол		**КМ1**	по образцу	инженерная доска · аналог по хар.				3,5 м²
	плинтус		**К4**	Farrow & Ball No. 241	МДФ · в цвет Farrow & Ball			67	4,5 м

Перечень выкрасов на согласование

№	Код	Бренд / веер	Пом. / стена	Подложка	Формат	Статус
1	No. 241	Farrow & Ball	1, 4, 5, 6, 8	ГКЛ с грунтом; МДФ под эмаль	600×1000; 300×600	к выполнению
2	No. 30	Farrow & Ball	1 А, 4 А, 6 А	ГКЛ с грунтом	600×1000	к выполнению
3	V503	Tikkurila	1, 2, 3, 4, 5, 6, 7, 8	ГКЛ с грунтом; МДФ под эмаль	600×1000; 300×600	к выполнению

Примечания

1. Цвет на листе и на экране — ориентир. До покраски — выкрас на объекте: не меньше А3 (или лист ГКЛ), на грунте под эту краску, не на белой шпаклёвке, в 2 слоя; на обороте — код, бренд, веер, дата. Смотреть днём и вечером, рядом с образцами пола и плитки; к основному цвету стен — ещё 2 соседних оттенка. Красить только в цвет утверждённого выкраса.
2. Краску заказывать по коду из графы «Система и код цвета» у бренда этого кода, не «аналогом» другого; весь объём одного кода — одной партией, колеруемую краску — за один проход машины.
3. Площади — те же, что в ведомости отделки (лист С1); сколько краски заказать — в спецификации отделочных материалов (лист С3).

Схема квартиры: цвет стен и акценты (б/м)

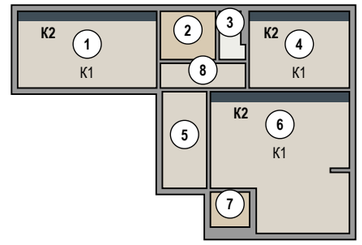


Схема палитры проекта

Стиль: Современный (контемпорари) · схема: аналоговая

основной	основной	второстепенный	акцентный
Tikkurila V503	**Farrow & Ball No. 241**	**Tikkurila H487**	**Farrow & Ball No. 30**
Winter LRV 86 потолок 1,2,3,4,5,6,7,8; стены 3; плинтус 3; текстиль/декор 1,4,6	Skimming Stone LRV 67 стены 1,4,5,6,8; плинтус 1,4,5,6,8	Pumice LRV 57 текстиль/декор 1,4,6	Hague Blue LRV 7 акцент 1,4,6; текстиль/декор 1,4,6

План 60/30/10

60%	30%	10%

Окраска, факт — по площади стен, акцентов, потолков

85%	15%

окрашено всего 251 м²; второстепенный тон несут мебель и текстиль

Текстиль и декор в цветах вне палитры проекта

- NCS S 3005-Y20R тёплый тауп-серый — пом. 1 (Т3)
- Tikkurila V484 Driftwood — пом. 4 (Т9), 6 (Т15, Т16, Т19)
- Farrow & Ball No. 229 Elephant's Breath — пом. 4 (Т10)
- Farrow & Ball No. 47 Green Smoke — пом. 4 (Т11)


Условные обозначения

- **К1** Farrow & Ball No. 241 · Skimming Stone · Modern Emulsion · матовая · кл. 1
- **К2** Farrow & Ball No. 30 · Hague Blue · Modern Emulsion · матовая · кл. 1
- **К3** Tikkurila V503 · Winter · Anti-Reflex 2 · глубокомат. · кл. 2
- **К4** Farrow & Ball No. 241 · Skimming Stone · МДФ
- **К5** Tikkurila V503 · Winter · Luja 7 · матовая · кл. 1
- **К6** Tikkurila V503 · Winter · Harmony · матовая · кл. 1
- **К7** Tikkurila V503 · Winter · МДФ
- дерево (доска, паркет, ламинат) — рисунок досок
- керамогранит, плитка, камень — сетка швов по формату
- **КМ1** аналог: инженерная доска, дуб натуральный, масло, 1-полосная, 14/4 мм
- **КМ2** плитка · аналог: керамогранит под травертин, матовый, 600×1200×9 мм
- **КМ3** аналог: керамогранит ректифицированный под травертин, матовый, 600×600×9 мм
- **КМ4** аналог: керамогранит ректифицированный под травертин, матовый, 600×1200×9 мм
- **КМ5** аналог: керамогранит под травертин, матовый, 1200×600×9 мм

К — краска, КМ — отделочный материал (тон КМ — по описанию, эталон — образец материала); кл. — класс истирания (1 — самый стойкий к мытью); LRV — светлота цвета: 0 — чёрный, 100 — белый

					Проект: Трёхкомнатная квартира
	Лист	№ док.	Подпись	Дата	
Дизайнер	Кырлан А.С.			04.11.26	Колерная карта

Стадия	Лист	Листов
П	11	92

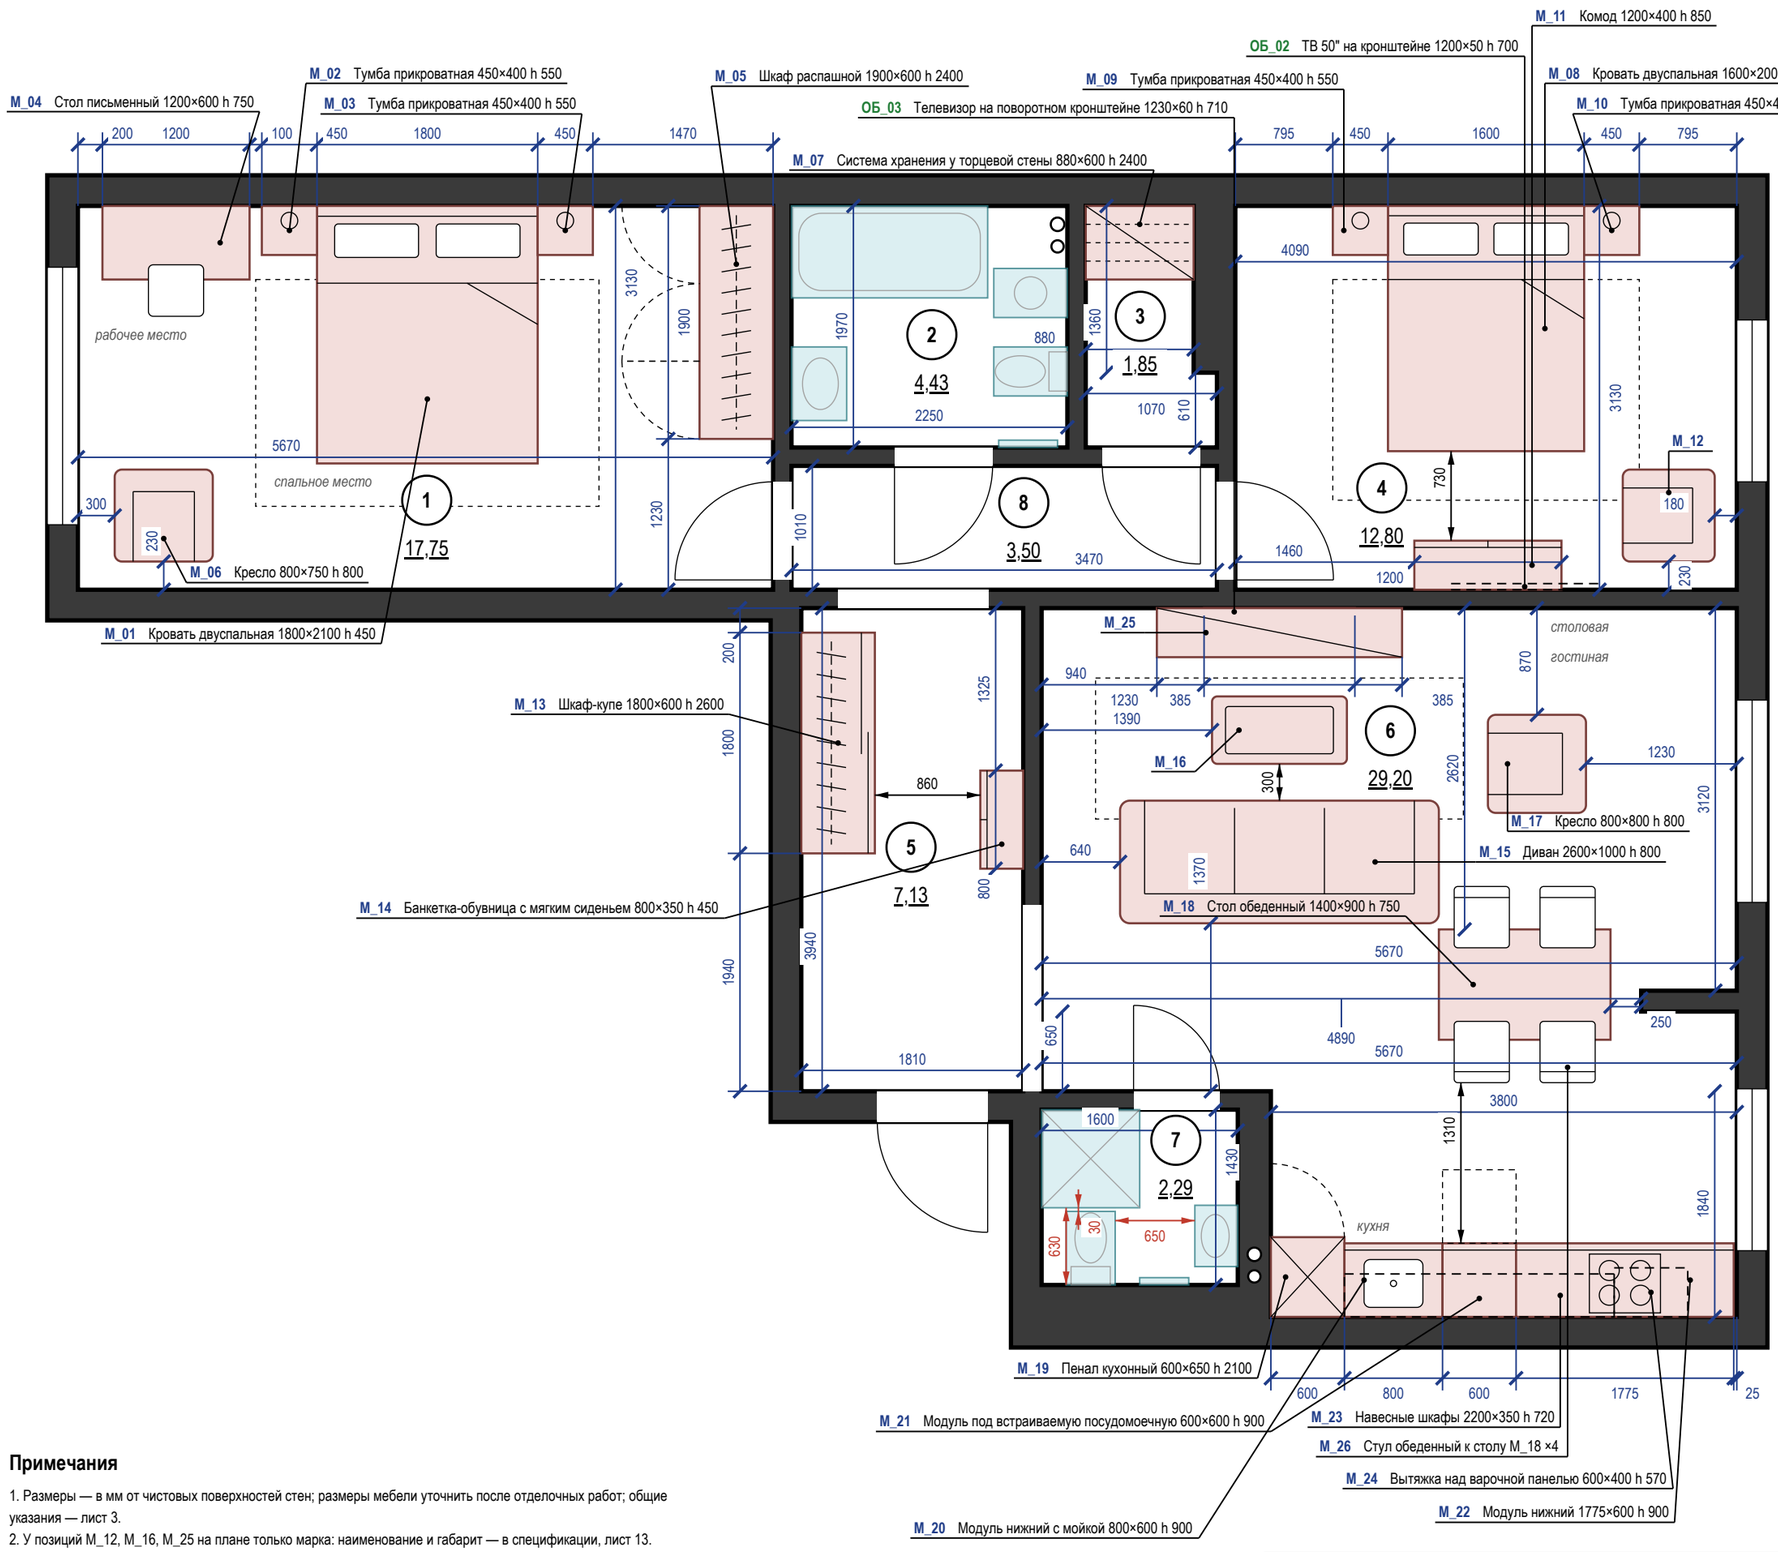

Экспликация помещений

лист 5 · на плане — номера в марках

Ведомость мебели и оборудования

Марка	Наименование	Ш×Г×В, мм	Пом.	Кол.
М_01	Кровать двуспальная	1800×2100×450	1	1
М_02	Тумба прикроватная	450×400×550	1	1
М_03	Тумба прикроватная	450×400×550	1	1
М_04	Стол письменный	1200×600×750	1	1
М_05	Шкаф распашной	1900×600×2400	1	1
М_06	Кресло	800×750×800	1	1
М_07	Система хранения у торцевой стены	880×600×2400	3	1
М_08	Кровать двуспальная	1600×2000×450	4	1
М_09	Тумба прикроватная	450×400×550	4	1
М_10	Тумба прикроватная	450×400×550	4	1
М_11	Комод	1200×400×850	4	1
М_12	Кресло для чтения у окна	750×750×800	4	1
ОБ_02	ТВ 50" на кронштейне	1200×50×700	4	1
М_13	Шкаф-купе	1800×600×2600	5	1
М_14	Банкетка-обувница с мягким сиденьем	800×350×450	5	1
ОБ_03	Телевизор на поворотном кронштейне	1230×60×710	6	1
М_15	Диван	2600×1000×800	6	1
М_16	Стол журнальный	1100×550×400	6	1
М_17	Кресло	800×800×800	6	1
М_18	Стол обеденный	1400×900×750	6	1
М_19	Пенал кухонный	600×650×2100	6	1
М_20	Модуль нижний с мойкой	800×600×900	6	1
М_21	Модуль под встраиваемую посудомоечную	600×600×900	6	1
М_22	Модуль нижний	1775×600×900	6	1
М_23	Навесные шкафы	2200×350×720	6	1
М_24	Вытяжка над варочной панелью	600×400×570	6	1
М_25	Тумба под ТВ подвесная	2000×400×400	6	1
М_26	Стул обеденный к столу М_18	450×500×820	6	4

Ш — вдоль стены (изголовья), Г — от стены (длина кровати)

Материалы, модели, допуск замены — лист 13

Примечания

1. Размеры — в мм от чистовых поверхностей стен; размеры мебели уточнить после отделочных работ; общие указания — лист 3.
2. У позиций М_12, М_16, М_25 на плане только марка: наименование и габарит — в спецификации, лист 13.
3. Стулья обеденной группы (М_26 — 4 шт.) показаны в рабочем положении, задвинутыми под столешницу на 150 мм.

	Лист	№ док.	Подпись	Дата
Дизайнер	Кырлан А.С.			04.11.26

Проект: Трёхкомнатная квартира — М 1:50

План размещения мебели и оборудования

Стадия	Лист	Листов
П	12	92

Поз.	Наименование и техническая характеристика	Тип, марка, обозначение документа, опросного листа	Код продукции	Поставщик	Ед. измерения	Кол.	Масса 1 ед., кг	Примечание
	Мебель встроенная и корпусная (изготовление по чертежам мебельщика)							
М_05	Шкаф распашной; корпус ЛДСП 16 мм; фасады — МДФ 18 мм, эмаль матовая; цвет фасадов — в цвет стен (Farrow & Ball No. 241); Ш×Г×В 1900×600×2400 мм			изготовление на заказ	шт.	1		пом. 1; крепление к стене
М_07	Система хранения у торцевой стены: штанга вдоль стены, полки, ящики; каркас и полки — ЛДСП 16 мм, декор «дуб натуральный»; без фасадов; Ш×Г×В 880×600×2400 мм			изготовление на заказ	шт.	1		пом. 3; крепление к стене
М_13	Шкаф-купе; корпус ЛДСП 16 мм; фасады — ЛДСП 10 мм в алюминиевом профиле; Ш×Г×В 1800×600×2600 мм			изготовление на заказ	шт.	1		пом. 5
М_19	Пенал кухонный, холодильник; корпус ЛДСП 16 мм; фасады — МДФ 18 мм, эмаль матовая; цвет фасадов — в цвет стен (Farrow & Ball No. 241); Ш×Г×В 600×650×2100 мм			изготовление на заказ	шт.	1		пом. 6; крепление к стене
М_20	Модуль нижний с мойкой; корпус ЛДСП 16 мм; фасады — МДФ 18 мм, эмаль матовая; цвет фасадов — в цвет стен (Farrow & Ball No. 241); Ш×Г×В 800×600×900 мм			изготовление на заказ	шт.	1		пом. 6
М_21	Модуль под встраиваемую ПММ 60; без корпуса (ниша между соседними модулями); фасад на дверь машины — МДФ 18 мм, эмаль матовая; цоколь; цвет фасадов — в цвет стен (Farrow & Ball No. 241); Ш×Г×В 600×600×900 мм			изготовление на заказ	шт.	1		пом. 6
М_22	Модуль нижний: ящики, варочная панель, духовой шкаф, бутылочница; корпус ЛДСП 16 мм; фасады — МДФ 18 мм, эмаль матовая; цвет фасадов — в цвет стен (Farrow & Ball No. 241); Ш×Г×В 1775×600×900 мм			изготовление на заказ	шт.	1		пом. 6
М_23	Навесные шкафы, 3 секции; корпус ЛДСП 16 мм; фасады — МДФ 18 мм, эмаль матовая; цвет фасадов — в цвет стен (Farrow & Ball No. 241); Ш×Г×В 2200×350×720 мм			изготовление на заказ	шт.	1		пом. 6
М_24	Вытяжка над варочной панелью; корпус ЛДСП 16 мм; фасады — МДФ 18 мм, эмаль матовая; цвет фасадов — в цвет стен (Farrow & Ball No. 241); Ш×Г×В 600×400×570 мм			изготовление на заказ	шт.	1		пом. 6
	Мебель покупная							
М_01	Кровать двуспальная; мягкое изголовье, обивка — ткань, цвет Tikkurila H487; Ш×Г×В 1800×2100×450 мм			аналог по характеристикам	шт.	1		пом. 1; замена ≤ габарита
М_02, М_03, М_09, М_10	Тумба прикроватная; шпон, дуб натуральный, матовое масло; Ш×Г×В 450×400×550 мм			аналог по характеристикам	шт.	4		пом. 1, 4; замена ≤ габарита
М_04	Стол письменный; шпон, дуб натуральный, матовое масло; Ш×Г×В 1200×600×750 мм			аналог по характеристикам	шт.	1		пом. 1; замена ≤ габарита
М_06	Кресло; обивка — ткань, цвет Tikkurila H487; Ш×Г×В 800×750×800 мм			аналог по характеристикам	шт.	1		пом. 1; замена ≤ габарита
М_08	Кровать двуспальная; мягкое изголовье, обивка — ткань, цвет Tikkurila H487; Ш×Г×В 1600×2000×450 мм			аналог по характеристикам	шт.	1		пом. 4; замена ≤ габарита
М_11	Комод; шпон, дуб натуральный, матовое масло; Ш×Г×В 1200×400×850 мм			аналог по характеристикам	шт.	1		пом. 4; крепление к стене; замена ≤ габарита
М_12	Кресло для чтения у окна; обивка — ткань, цвет Tikkurila H487; Ш×Г×В 750×750×800 мм			аналог по характеристикам	шт.	1		пом. 4; замена ≤ габарита
ОБ_02	ТВ 50" на кронштейне над комодом М_11; шпон, дуб натуральный, матовое масло; Ш×Г×В 1200×50×700 мм			аналог по характеристикам	шт.	1		пом. 4; замена ≤ габарита
М_14	Банкетка-обувница с мягким сиденьем, над ней настенная вешалка с полкой (низ 1650); шпон, дуб натуральный, матовое масло; Ш×Г×В 800×350×450 мм			аналог по характеристикам	шт.	1		пом. 5; замена ≤ габарита
М_15	Диван; обивка — ткань, цвет Tikkurila H487; Ш×Г×В 2600×1000×800 мм			аналог по характеристикам	шт.	1		пом. 6; замена ≤ габарита
М_16	Стол журнальный; шпон, дуб натуральный, матовое масло; Ш×Г×В 1100×550×400 мм			аналог по характеристикам	шт.	1		пом. 6; замена ≤ габарита

Примечания

1. Позиции мебели совпадают с марками на плане расстановки; размеры Ш×Г×В — Ш вдоль стены, Г от стены.
2. Размеры и привязки плана расстановки — в мм от чистовых поверхностей стен: слой штукатурки 20 мм по блоку и 5 мм шпаклёвки по ГКЛ учтён; привязки — от стен и углов помещения, а не от другой мебели.
3. План расстановки не является документацией для изготовления мебели. Встроенная и корпусная мебель изготавливается по чертежам мебельщика после контрольного обмера (после штукатурки); «стена в стену» — с зазором 10 мм с каждой стороны или с компенсаторами; графы «Тип, марка» и «Код продукции» для неё не заполняются (ГОСТ 21.110-2013).
4. Покупные изделия — аналог по характеристикам: заменять только на изделия не больше указанного габарита и того же материала и цвета.
5. Материал и цвет, не указанные в данных изделия, приняты по концепции: тон дерева — по полу, обивка — по вторичному цвету палитры; образцы согласовать до заказа.
6. Масса 1 ед. для изделий до 25 кг не указывается. Техника — по монтажным схемам изготовителя; выводы — по листам ЭОМ и ВК.

					Проект: Трёхкомнатная квартира
	Лист	№ док.	Подпись	Дата	
Дизайнер	Кырлан А.С.			04.11.26	Спецификация мебели и оборудования
					Стадия: П; Лист: 13; Листов: 92

Поз.	Наименование и техническая характеристика	Тип, марка, обозначение документа, опросного листа	Код продукции	Поставщик	Ед. измерения	Кол.	Масса 1 ед., кг	Примечание
М_17	Кресло; обивка — ткань, цвет Tikkurila H487; Ш×Г×В 800×800×800 мм			аналог по характеристикам	шт.	1		пом. 6; замена ≤ габарита
М_18	Стол обеденный; шпон, дуб натуральный, матовое масло; Ш×Г×В 1400×900×750 мм			аналог по характеристикам	шт.	1		пом. 6; замена ≤ габарита
М_25	Тумба под ТВ подвесная, низ на 300 мм от пола; шпон, дуб натуральный, матовое масло; Ш×Г×В 2000×400×400 мм			аналог по характеристикам	шт.	1		пом. 6; крепление к стене; замена ≤ габарита
М_26	Стул обеденный к столу М_18; обивка — ткань, цвет Tikkurila H487; каркас — дуб натуральный; Ш×Г×В 450×500×820 мм			аналог по характеристикам	шт.	4		пом. 6; замена ≤ габарита
ОБ_03	Телевизор на поворотном кронштейне, центр экрана на 1150 мм от пола; диагональ 55"; крепление — настенный кронштейн по паспорту модели; Ш×Г×В 1230×60×710 мм			аналог по характеристикам	шт.	1		пом. 6; замена ≤ габарита
	Техника встраиваемая и бытовая (покупные изделия), светильники под розетки							
	Стиральная машина, место по листу ВК (ОБ_01); Ш×Г 400×600 мм	аналог по характеристикам: вертикальная загрузка, в плане 400 × 600 мм (ширина × глубина), по листу ВК		по выбору заказчика до изготовления мебели	шт.	1		пом. 2; по схеме изготовителя
	Холодильник встраиваемый, в модуле М_19	аналог по характеристикам: полновстраиваемый под фасад, ниша 1780 × 560 × 550 мм, вентиляция решётка в цоколе, выход сверху		по выбору заказчика до изготовления мебели	шт.	1		пом. 6; по схеме изготовителя
	Посудомоечная машина встраиваемая, в модуле М_21; ниша 600 мм	аналог по характеристикам: полновстраиваемая 60 см под фасад, ниша 600 × 862 мм, навеска фасада в комплекте		по выбору заказчика до изготовления мебели	шт.	1		пом. 6; по схеме изготовителя
	Варочная панель встраиваемая, индукционная, в модуле М_22	аналог по характеристикам: индукционная 60 см, вырез 560 × 490 мм по шаблону модели		по выбору заказчика до изготовления мебели	шт.	1		пом. 6; по схеме изготовителя
	Духовой шкаф встраиваемый, в модуле М_22	аналог по характеристикам: 60 см, лицевая панель 595 мм, ниша 560 × 600, глубина ≥ 550 мм, вентиляция за прибором		по выбору заказчика до изготовления мебели	шт.	1		пом. 6; по схеме изготовителя
	Вытяжка, в модуле М_24	аналог по характеристикам: производительность — по расчёту ОВ, шум ≤ 55 дБ(А)		по выбору заказчика до изготовления мебели	шт.	1		пом. 6; по схеме изготовителя
	Торшер, у поз. М_06; абажур — ткань или опаловое стекло; лампа 2700 K			аналог по характеристикам	шт.	1		пом. 1; розетка Р5 (ЭОМ)
	Торшер, у поз. М_25; абажур — ткань или опаловое стекло; лампа 2700 K			аналог по характеристикам	шт.	1		пом. 6; розетка Р21 (ЭОМ)
	Текстиль							
Т1	Портьеры-волна; лён 100 %; цвет Tikkurila H487; карниз 2500 мм, высота 2610 мм, сборка 2			аналог по характеристикам	шт.	2		пом. 1
Т2	Тюль; полиэстер 100 %; цвет Tikkurila V503; карниз 2500 мм, высота 2610 мм, сборка 2,5			аналог по характеристикам	шт.	1		пом. 1
Т3	Ковёр под кроватью; шерсть 80 %, хлопок 20 %; цвет NCS S 3005-Y20R; 2800×1850 мм			аналог по характеристикам	шт.	1		пом. 1; с подложкой
Т4	Подушки декоративные на кровать; лён 100 %; цвет Tikkurila H487			аналог по характеристикам	шт.	3		пом. 1
Т5	Подушки на кровать, акцент; хлопковый бархат 100 %; цвет Farrow & Ball No. 30			аналог по характеристикам	шт.	2		пом. 1
Т6	Плед на кровать; шерсть мериноса 100 %; цвет Farrow & Ball No. 30			аналог по характеристикам	шт.	1		пом. 1

					Проект: Трёхкомнатная квартира
	Лист	№ док.	Подпись	Дата	Спецификация мебели и оборудования (продолжение)
Дизайнер	Кырлан А.С.			04.11.26	

Стадия	Лист	Листов
П	14	92

Поз.	Наименование и техническая характеристика	Тип, марка, обозначение документа, опросного листа	Код продукции	Поставщик	Ед. измерения	Кол.	Масса 1 ед., кг	Примечание
Т7	Портьеры-волна; лён 100 %; цвет Tikkurila H487; карниз 1820 мм, высота 2610 мм, сборка 2			аналог по характеристикам	шт.	2		пом. 4
Т8	Тюль; полиэстер 100 %; цвет Tikkurila V503; карниз 1820 мм, высота 2610 мм, сборка 2,5			аналог по характеристикам	шт.	1		пом. 4
Т9	Ковёр под кроватью; шерсть 100 %; цвет Tikkurila V484; 2500×1800 мм			аналог по характеристикам	шт.	1		пом. 4; с подложкой
Т10	Подушки декоративные на кровать; букле (шерсть 60 %, полиэстер 40 %); цвет Farrow & Ball No. 229			аналог по характеристикам	шт.	3		пом. 4
Т11	Подушки на кровать, акцент; хлопковый бархат 100 %; цвет Farrow & Ball No. 47			аналог по характеристикам	шт.	2		пом. 4
Т12	Плед на кровать; шерсть мериноса 100 %; цвет Farrow & Ball No. 30			аналог по характеристикам	шт.	1		пом. 4
Т13	Портьеры-волна (гостиная); лён 70 %, вискоза 30 %; цвет Tikkurila H487; карниз 2250 мм, высота 2610 мм, сборка 2			аналог по характеристикам	шт.	2		пом. 6
Т14	Тюль (гостиная); полиэстер 100 %; цвет Tikkurila V503; карниз 2250 мм, высота 2610 мм, сборка 2,5			аналог по характеристикам	шт.	1		пом. 6
Т15	Римская штора (кухня); лён 100 %; цвет Tikkurila V484; карниз 1400 мм, высота 1620 мм			аналог по характеристикам	шт.	1		пом. 6
Т16	Ковёр в зоне отдыха; шерсть 100 %; цвет Tikkurila V484; 3000×1150 мм			аналог по характеристикам	шт.	1		пом. 6; с подложкой
Т17	Подушки на диван; букле (шерсть 60 %, полиэстер 40 %); цвет Tikkurila H487			аналог по характеристикам	шт.	3		пом. 6
Т18	Подушки на диван, акцент; хлопковый бархат 100 %; цвет Farrow & Ball No. 30			аналог по характеристикам	шт.	2		пом. 6
Т19	Плед на диван; альпака 50 %, шерсть 50 %; цвет Tikkurila V484			аналог по характеристикам	шт.	1		пом. 6
	Декор							
ДК1	Картина над кроватью: абстракция, холст, тонкая рама из дуба; 1200×700 мм; низ на 1300 мм от пола			аналог по характеристикам	шт.	1	4	пом. 1; крепление к стене
ДК2	Зеркало над умывальником, влагостойкое; 600×750 мм; низ на 1100 мм от пола			аналог по характеристикам	шт.	1	4	пом. 2; крепление к стене
ДК3	Картина над кроватью: графика в паспарту, рама — дуб; 1000×700 мм; низ на 1300 мм от пола			аналог по характеристикам	шт.	1	4	пом. 4; крепление к стене
ДК4	Зеркало в рост в тонкой чёрной раме; рама — чёрный матовый; 600×1600 мм; низ на 300 мм от пола			аналог по характеристикам	шт.	1	12	пом. 4; крепление: анкер для пустотелых оснований, 4 шт.
ДК5	Зеркало; рама — чёрный матовый; 800×1800 мм; низ на 550 мм от пола			аналог по характеристикам	шт.	1	18	пом. 5; крепление: анкер, 4 шт.
ДК6	Картина: крупная абстракция в тёплой гамме, холст на подрамнике; 1200×900 мм; центр на 1550 мм от пола			аналог по характеристикам	шт.	1	6	пом. 6; крепление: анкер, 2 шт.
ДК7	Растение в кашпо; 450×450 мм			аналог по характеристикам	шт.	1		пом. 6
ДК8	Ваза керамическая с ветками на обеденном столе; 200×350 мм; на M_18			аналог по характеристикам	шт.	1		пом. 6
ДК9	Зеркало над умывальником, влагостойкое; 500×700 мм; низ на 1100 мм от пола			аналог по характеристикам	шт.	1	4	пом. 7; крепление к стене

					Проект: Трёхкомнатная квартира	
	Лист	№ док.	Подпись	Дата		
Дизайнер	Кырлан А.С.			04.11.26	Спецификация мебели и оборудования (продолжение)	Стадия: П; Лист: 15; Листов: 92

Ведомость изделий

Марка	Наименование	Пом.	Ш×Г×В, мм	Корпус	Фасад	Кромка, мм	Кол.
M_05	Шкаф распашной	1	1900×600×2400	ЛДСП 16	МДФ 18 мм, эмаль матовая	0,4 / 2	1
M_07	Система хранения	3	880×600×2400	ЛДСП 16	без фасадов	0,4 / 2	1
M_13	Шкаф-купе	5	1800×600×2600	ЛДСП 16	ЛДСП 10 мм в алюминиевом профиле	0,4 / 2	1
M_22	Модуль нижний: карго, духовой шкаф, ящики, варочная	6	1775×600×900	ЛДСП 16	МДФ 18 мм, эмаль матовая	0,4 / 2	1
M_24	Модуль навесной: полки	6	600×400×570	ЛДСП 16	МДФ 18 мм, эмаль матовая	0,4 / 2	1
M_23	Модуль навесной: полки, сушка	6	2200×350×720	ЛДСП 16	МДФ 18 мм, эмаль матовая	0,4 / 2	1
M_21	Модуль под ПММ 60: без корпуса, фасад на дверь машины	6	600×600×900	без корпуса	МДФ 18 мм, эмаль матовая — на дверь машины (навеска из её комплекта), цоколь		1
M_20	Модуль нижний: мойка	6	800×600×900	ЛДСП 16	МДФ 18 мм, эмаль матовая	0,4 / 2	1
M_19	Пенал: холодильник встр.	6	600×650×2100	ЛДСП 16	МДФ 18 мм, эмаль матовая	0,4 / 2	1

Ведомость встраиваемой техники

Поз.	Прибор	Ниша, вырез, мм	Вентиляция	Питание	Схема
M_22.2	Духовой шкаф встраиваемый, 60 см	ниша 560 × 600, глубина ≥ 550	зазор за шкафом, вырез в задней стенке	ЭВ2: M_22.2, H=150 — под духовым шкафом, доступ через ящик	по модели
M_22.2	Варочная панель индукционная, 60 см	вырез в столешнице 560 × 490		ЭВ1: M_22.3, H=600 — в соседнем модуле, за ящиком	по модели
M_21	Посудомоечная машина встраиваемая, 60 см	ниша 600 × 862 (от пола до низа столешницы)	зазор в цоколе, по схеме	Р32: M_22.3, H=300 — в соседнем модуле, за ящиком	по модели
M_20	Мойка врезная / подстольная с сифоном	вырез по шаблону, ориентир 700 × 480		смеситель — выводы ВК	по модели
M_19	Холодильник встраиваемый, ниша 1780	ниша 1780 × 560 × 550	решётка в цоколе, канал за корпусом, выход сверху	Р25: M_19, H=2000 — над нишей холодильника, съёмная панель	по модели
M_24	Вытяжка встраиваемая в навесной модуль, 60 см	низ ≥ 650 над панелью	воздуховод к вентканалу, короб до потолка	ЭВ3: M_24, H=2200 — в навесном модуле	по модели

Ведомость фурнитуры

№	Фурнитура	Тип, размер	Изделия	Кол.
1	Петля накладная 110° с доводчиком	чашка 35 мм	M_05, M_24, M_23, M_20, M_19	51
2	Полкодержатель с фиксацией	ø5 мм	M_05, M_07, M_13, M_24, M_23, M_19	92
3	Штанга овальная 30×15, L = 926	+ 2 держателя	M_05	1
4	Опора регулируемая с цоколем на клипсах	ход 20 мм	M_05, M_07, M_13	22
5	Анкер по основанию стены	по таблице крепежа	M_05, M_07, M_13, M_24, M_23	24
6	Уголок крепления к стене от опрокидывания	стальной	M_05, M_07, M_13, M_19	8
7	Штанга овальная 30×15, L = 416	+ 2 держателя	M_07	1
8	Система дверей купе: профиль, направляющие, ролики	на 2 двери	M_13	1
9	Ручка-профиль вертикальная	в цвет профиля	M_13	2
10	Штанга овальная 30×15, L = 876	+ 2 держателя	M_13	1
11	Полка для обуви выдвижная наклонная	ширина 876	M_13	3
12	Карго выдвижное 3-уровневое	ширина 325	M_22	1
13	Направляющие полного выдвижения с доводчиком NL 500	пара	M_22	4
14	Ручка-профиль	латунь матовая	M_22, M_24, M_23, M_21, M_20, M_19	19
15	Опора кухонная регулируемая 100–120 мм	+ клипса цоколя	M_22, M_20, M_19	16
16	Навес регулируемый для навесного шкафа	пара на секцию	M_24, M_23	4
17	Шина монтажная	L = 540	M_24	1
18	Сушка для посуды в шкаф	ширина 800	M_23	1
19	Шина монтажная	L = 2140	M_23	1
20	Комплект навески фасада ПММ	из поставки машины	M_21	1


Примечания

1. Модели техники выбирает заказчик до изготовления мебели; ниши, вырезы и вентиляция — по монтажной схеме выбранной модели (условие гарантии), её номер вносится в ведомость.
2. Количество фурнитуры — по чертежам изделий; запас крепежа 5 %. Аналоги — по характеристикам (доводчик, нагрузка, ход).
3. Цвет корпусов, фасадов и профилей — по колерной карте проекта. Кромка — скрытые / видимые торцы, мм.


					Проект: Трёхкомнатная квартира
	Лист	№ док.	Подпись	Дата	Ведомости изделий, техники и фурнитуры
Дизайнер	Кырлан А.С.			04.11.26	

Стадия	Лист	Листов
П	16	92


Фрагмент 1. Ванная (пом. 2)

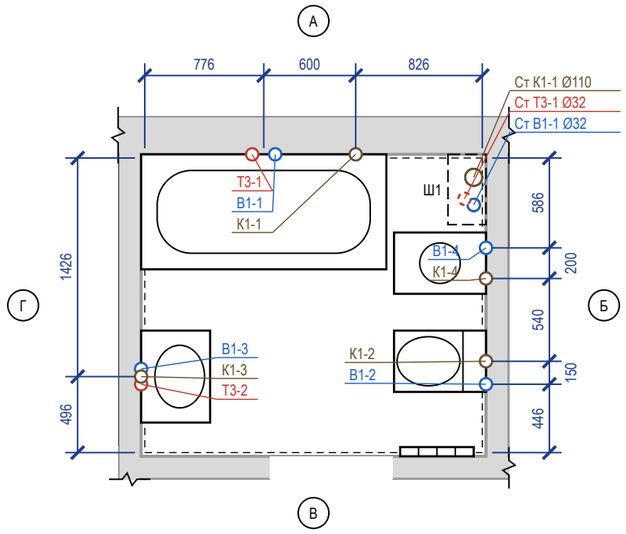

Фрагмент 2. Кухня-гостиная (пом. 6)

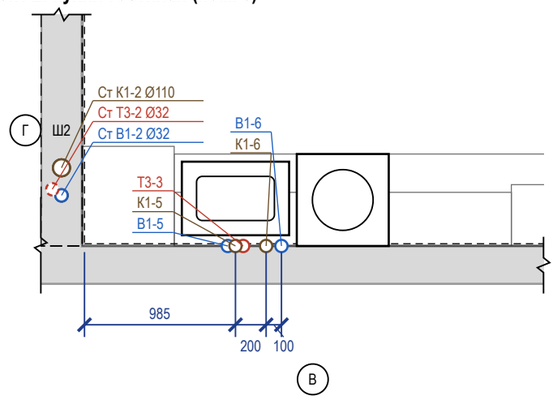

Фрагмент 3. Санузел 2 (пом. 7)

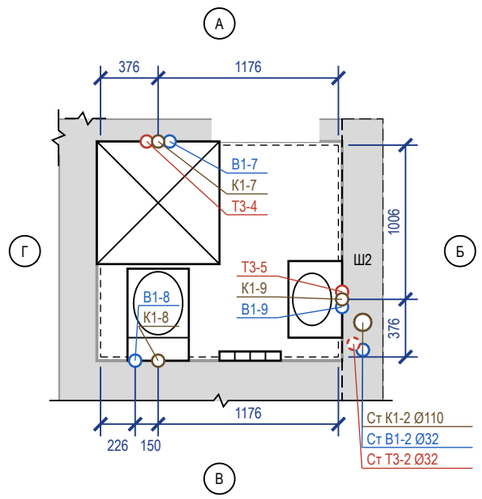

Ведомость привязок выводов

Код	Прибор	Ø	H, мм	Привязка от чист. стен, мм	Прим.
В1-1	С_01 ванна	½"	800	ст. А: 851 от Г	межос. 150
Т3-1	С_01 ванна	½"	800	ст. А: 701 от Г	межос. 150
К1-1	С_01 ванна	Ø50	50	ст. А: 826 от Б	
В1-2	С_02 унитаз подвесной	½"	250	ст. Б: 446 от В	в раме инсталляции
К1-2	С_02 унитаз подвесной	Ø110	220	ст. Б: 596 от В	
В1-3	С_03 умывальник	½"	600	ст. Г: 546 от В	межос. 100
Т3-2	С_03 умывальник	½"	600	ст. Г: 446 от В	межос. 100
К1-3	С_03 умывальник	Ø50	500	ст. Г: 496 от В	
В1-4	ОБ_01 стиральная машина	½"	600	ст. Б: 586 от А	кран машины
К1-4	ОБ_01 стиральная машина	Ø50	600	ст. Б: 786 от А	
В1-5	С_05 мойка кухонная	½"	600	ст. В: 935 от Г	межос. 100
Т3-3	С_05 мойка кухонная	½"	600	ст. В: 1035 от Г	межос. 100
К1-5	С_05 мойка кухонная	Ø50	400	ст. В: 985 от Г	
В1-6	ОБ_04 посудомоечная машина	½"	550	ст. В: 1285 от Г	кран ПММ в шкафу мойки
К1-6	ОБ_04 посудомоечная машина	Ø40	550	ст. В: 1185 от Г	слив ПММ в шкафу мойки
В1-7	С_06 душ	½"	1200	ст. А: 451 от Г	межос. 150
Т3-4	С_06 душ	½"	1200	ст. А: 301 от Г	межос. 150
К1-7	С_06 душ	Ø50	70	ст. А: 376 от Г	сифон поддона
В1-8	С_07 унитаз подвесной	½"	250	ст. В: 226 от Г	в раме инсталляции
К1-8	С_07 унитаз подвесной	Ø110	220	ст. В: 376 от Г	
В1-9	С_08 умывальник	½"	600	ст. Б: 326 от В	межос. 100
Т3-5	С_08 умывальник	½"	600	ст. Б: 426 от В	межос. 100
К1-9	С_08 умывальник	Ø50	500	ст. Б: 376 от В	

Условные обозначения


- вывод В1 (код — в ведомости привязок)
- вывод Т3 (код — в ведомости привязок)
- вывод К1 (код — в ведомости привязок)
- сантехприбор по расстановке (габарит модели)
- чистовая поверхность стены (от неё привязки)
- стояк «Ст К1-N / Ст В1-N» (ГОСТ 21.601), Ø мм
- стояк Т3 не на обмере — принят в шахте рядом со Ст В1, сверить
- шахта / короб стояков, люк 300×400
- линия обрыва (граница фрагмента)
- А — обозначение стены А–Г (как на развёртках)

Примечания


1. Привязки выводов даны от чистовых поверхностей стен (облицовка на сторону: ванная — 24 мм (штукатурка 10 + клей 5 + плитка 9); кухня-гостиная — 24 мм (фартук: штукатурка 10 + клей 5 + плитка 9); санузел 2 — 24 мм (штукатурка 10 + клей 5 + плитка 9)); эти же грани — на развёртках и в раскладке плитки. Высоты — от чистого пола помещения.
2. До черновой разводки сверить по паспорту выбранного прибора (смеситель, инсталляция, сифон).
3. Горячая вода (Т3) — слева от холодной (В1), если смотреть на прибор. Допуск установки выводов: ±5 мм в группе, ±20 мм у отдельно стоящих.
4. Расчёт систем водоснабжения и канализации и подбор оборудования выполняет проектная организация; лист задаёт места и высоты выводов.
5. Посудомоечная машина ОБ_04: кран и слив — отдельными выводами в шкафу мойки (не за машиной), до машины ≤ 1500 мм.
6. Ст Т3-1, Ст Т3-2 на обмере не показаны: приняты рядом с Ст В1-1, Ст В1-2 (в МКД стоят группой); положение сверить на объекте до разметки.
7. Стояки в коробах/шахтах Ш1, Ш2 не замоноличивать; стояк К1 в коробе — звукоизоляция стояка в коробе без жёсткого контакта с трубой; к арматуре и ревизиям — люк не меньше 300×400.

					Проект: Трёхкомнатная квартира — М 1:40
	Лист	№ док.	Подпись	Дата	
Дизайнер	Кырлан А.С.			04.11.26	План выводов сантехники
					Стадия: П; Лист: 17; Листов: 92


План квартиры (М 1:200)

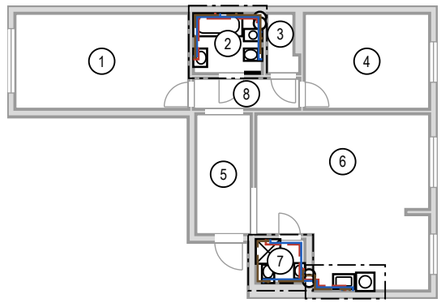


Фр. 2. Кухня-гостиная (М 1:25)

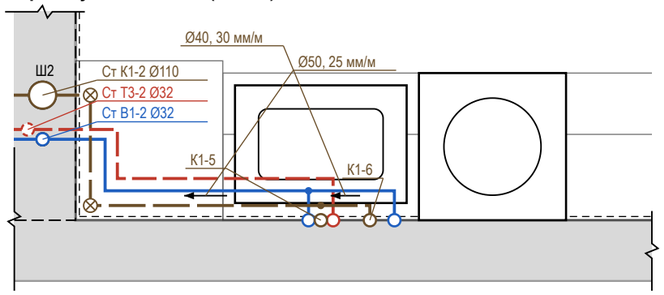

Фр. 1. Ванная (М 1:25)

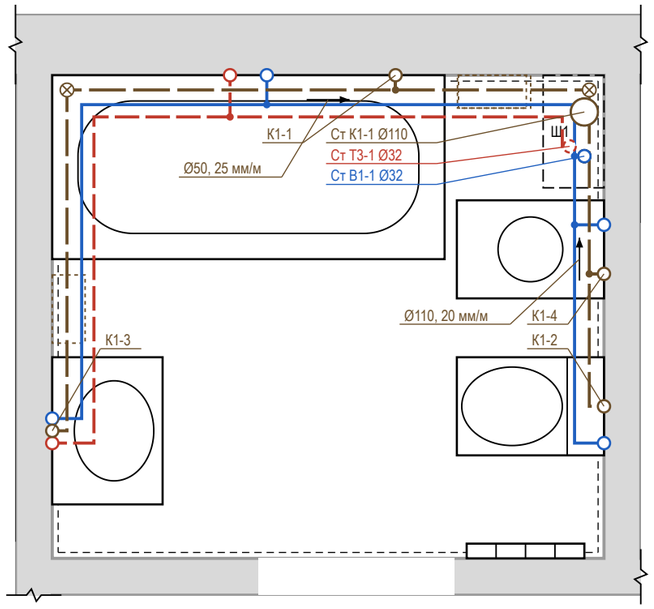

Фр. 3. Санузел 2 (М 1:25)

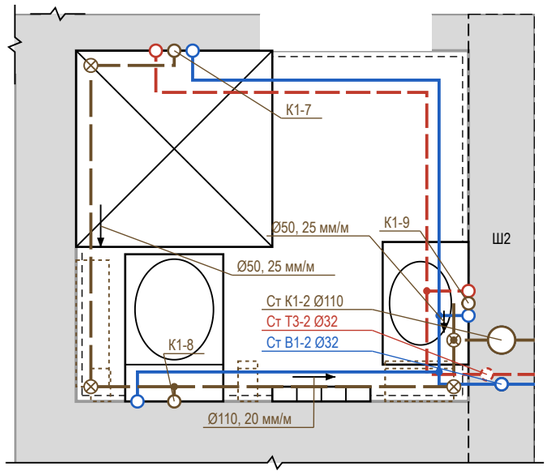

Условные обозначения


- В1 — водопровод хозяйственно-питьевой (ХВС), PP-R Ø20
- Т3 — горячее водоснабжение, подача (ГВС), PP-R Ø20
- К1 — канализация бытовая
- направление уклона К1 / пола: Ø, мм на 1 м
- ⊗ ревизия (прочистка) К1 — доступ сохранить
- • тройник (ответвление к прибору)
- короб К1 над чистым полом (ГКЛВ под плитку)
- ○ вывод В1 (код — в ведомости привязок)
- ○ вывод Т3 (код — в ведомости привязок)
- ○ вывод К1 (код — в ведомости привязок)
- ▭ сантехприбор по расстановке (габарит модели)
- ◯ стояк «Ст К1-N / Ст В1-N» (ГОСТ 21.601), Ø мм
- ◌ стояк Т3 не на обмере — принят в шахте рядом со Ст В1, сверить
- ▭ шахта / короб стояков, люк 300×400
- ⌇ линия обрыва (граница фрагмента)
- ▭ граница фрагмента на плане (Фр. N)

Профиль выпусков К1 (до врезки в стояк)

Выпуск	Прибор	Ø	L, м	i, мм/м	Δh, мм	Прокладка, мм
К1-8	С_07 унитаз подвесной	Ø110	1,58	20	32	короб 180×140
К1-2	С_02 унитаз подвесной	Ø110	1,28	20	26	над полом за приборами
К1-3	С_03 умывальник	Ø50	3,69	25	92	короб 180×110
К1-7	С_06 душ	Ø50	3,58	25	89	короб 170×110
К1-5	С_05 мойка кухонная	Ø50	1,65	25	41	над полом за приборами
К1-1	С_01 ванна	Ø50	0,96	25	24	короб 110×110
К1-4	ОБ_01 стиральная машина	Ø50	0,74	25	19	над полом за приборами
К1-9	С_08 умывальник	Ø50	0,41	25	10	над полом за приборами
К1-6	ОБ_04 посудомоечная машина	Ø40	1,84	30	55	над полом за приборами

Короб h×b: h — от чистого пола, b — от чистовой стены. Стяжка 35 мм — лист полов.

Узел ввода В1, Т3 (схема, без масштаба)

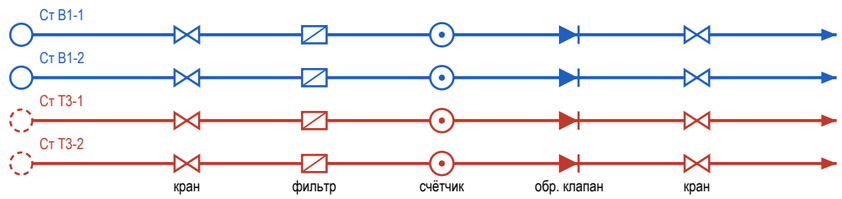

состав узла — по согласованию

⊗ Ст К1-1, Ст К1-2: ревизия на стояке — люк в коробе


Примечания

1. Трассы принципиальные, построены от стояков вдоль стен помещений; фактическое положение фиксируется исполнительной схемой с привязками (фото с рулеткой) до закрытия.
2. Уклон К1 не менее 1/d и не более 150 мм/м (СП 30.13330.2020, п. 19.1), приняты практические уклоны; поворот — двумя отводами 45°, ревизия после поворота, доступ сохранить. Стояк К1 в коробе — звукоизоляция стояка в коробе, без жёсткого контакта короба с трубой.
3. Решение по К1: стяжка 35 мм не укрывает трубы (нужно Ø + Δh + 45 мм) — выпуски идут над чистым полом вдоль стен: К1-2, К1-5, К1-4, К1-9, К1-6 — за приборами и в раме инсталляции; К1-8, К1-3, К1-7, К1-1 — в коробе ГКЛВ под плитку (размеры в профиле). Короба — на развёртках; отметку низа врезки в стояк замерить до черновых работ.
4. Состав узла ввода В1, Т3 — по согласованию: на схеме типовой узел — кран шаровой, фильтр, счётчик, обратный клапан, кран; состав и места не определены (записи реестра нет). Доступ к арматуре — через люк не меньше 300×400. Водопровод — в штробе стен или в коробах; трубы испытать давлением до закрытия (акт скрытых работ).
5. Расчёт систем, диаметры магистралей и подбор оборудования выполняет проектная организация; врезка и перенос стояков — по согласованию с управляющей организацией. Арматуру и привязки сверить по паспортам приборов.
6. Ст Т3-1, Ст Т3-2 на обмере не показаны: приняты рядом с Ст В1-1, Ст В1-2 (в МКД стоят группой); положение сверить на объекте до разводки.

					Проект: Трёхкомнатная квартира
	Лист	№ док.	Подпись	Дата	Схема разводки водопровода и канализации
Дизайнер	Кырлан А.С.			04.11.26	

Стадия	Лист	Листов
П	18	92

Схема В1 (М 1:50; по вертикали и горизонтали один масштаб, глубина — ×0,5 под 45°)

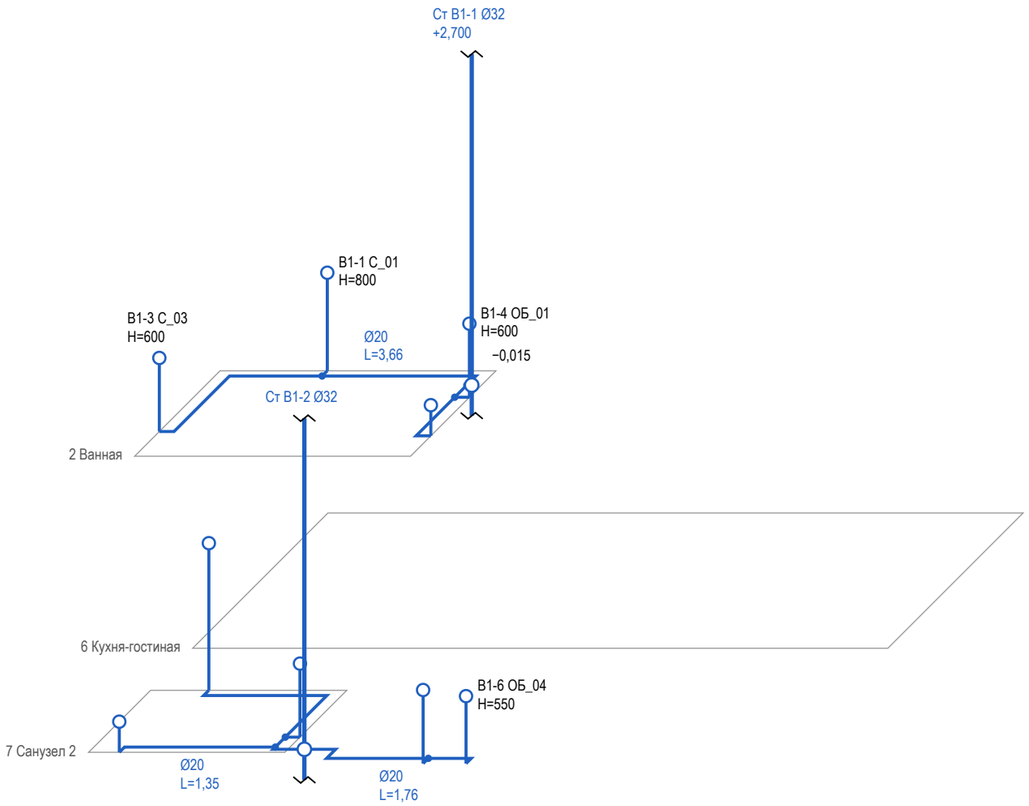

Условные обозначения


- В1 — водопровод хозяйственно-питьевой (ХВС), PP-R Ø20
- вывод В1 (код — в ведомости привязок)
- стояк «Ст К1-N / Ст В1-N» (ГОСТ 21.601), Ø мм
- стояк в плане (на отметке пола); вертикаль — стояк по высоте, разрыв — перекрытие
- тройник (ответвление к прибору)
- кран шаровой

Примечания

1. Схема В1 построена по тем же трассам, что план разводки: положение в плане сохранено, глубина — в масштабе ×0,5. Трассы принципиальные; фактическое положение фиксируется исполнительной схемой до закрытия.
2. Высоты Н — от чистого пола помещения, мм. Отметка прокладки магистрали В1 (в стяжке, в стене или по полу) в данных не задана: участки показаны на уровне пола условно (записи реестра нет).
3. Узел ввода В1 (кран, фильтр, счётчик, обратный клапан, кран) — на схеме разводки; состав узла ввода — по согласованию. Кран шаровой — на первом участке от стояка.
4. Трубы испытать давлением до закрытия (акт скрытых работ, опрессовка по СП 73.13330.2016).
5. Диаметры, высоты выводов и места кранов — по паспортам выбранных приборов и расчёту проектной организации.
6. Расчёт систем, диаметры магистралей и подбор оборудования выполняет проектная организация.

					Проект: Трёхкомнатная квартира		**М 1:50**
	Лист	№ док.	Подпись	Дата			
Дизайнер	Кырлан А.С.			04.11.26	Аксонометрическая схема В1 (холодное водоснабжение)	Стадия	Лист	Листов
						П	19	92

Схема Т3 (М 1:50; по вертикали и горизонтали один масштаб, глубина — ×0,5 под 45°)

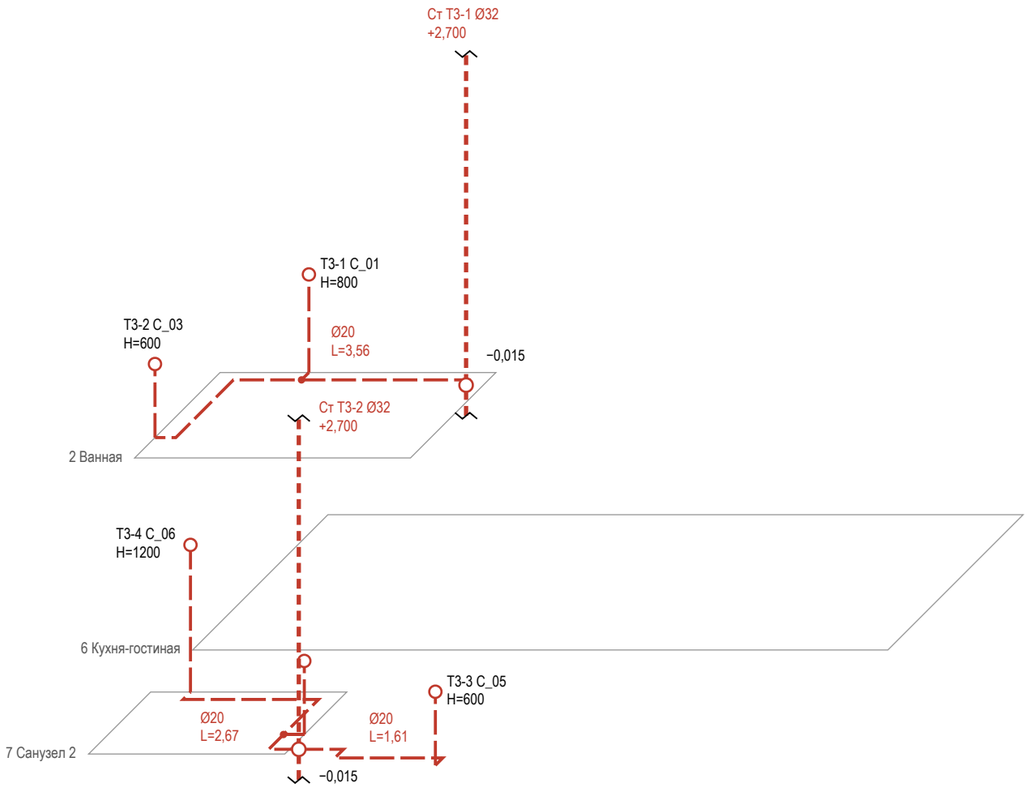

Условные обозначения


- Т3 — горячее водоснабжение, подача (ГВС), PP-R Ø20
- вывод Т3 (код — в ведомости привязок)
- стояк «Ст К1-N / Ст В1-N» (ГОСТ 21.601), Ø мм
- стояк в плане (на отметке пола); вертикаль — стояк по высоте, разрыв — перекрытие
- тройник (ответвление к прибору)
- кран шаровой
- стояк Т3 не на обмере — принят в шахте рядом со Ст В1, сверить

Примечания

1. Схема Т3 построена по тем же трассам, что план разводки: положение в плане сохранено, глубина — в масштабе ×0,5. Трассы принципиальные; фактическое положение фиксируется исполнительной схемой до закрытия.
2. Высоты Н — от чистого пола помещения, мм. Отметка прокладки магистрали Т3 (в стяжке, в стене или по полу) в данных не задана: участки показаны на уровне пола условно (записи реестра нет).
3. Узел ввода Т3 (кран, фильтр, счётчик, обратный клапан, кран) — на схеме разводки; состав узла ввода — по согласованию. Кран шаровой — на первом участке от стояка.
4. Циркуляция ГВС в данных не задана — циркуляционного трубопровода на схеме нет (записи реестра нет).
5. Ст Т3-1, Ст Т3-2 на обмере не показаны: приняты рядом с Ст В1-1, Ст В1-2 (в МКД стоят группой); положение сверить на объекте до разводки.
6. Трубы испытать давлением до закрытия (акт скрытых работ, опрессовка по СП 73.13330.2016).
7. Диаметры, высоты выводов и места кранов — по паспортам выбранных приборов и расчёту проектной организации.
8. Расчёт систем, диаметры магистралей и подбор оборудования выполняет проектная организация.

					Проект: Трёхкомнатная квартира	М 1:50
	Лист	№ док.	Подпись	Дата		
Дизайнер	Кырлан А.С.			04.11.26	Аксонометрическая схема Т3 (горячее водоснабжение)	Стадия: П; Лист: 20; Листов: 92

Схема К1 (М 1:50; по вертикали и горизонтали один масштаб, глубина — ×0,5 под 45°)

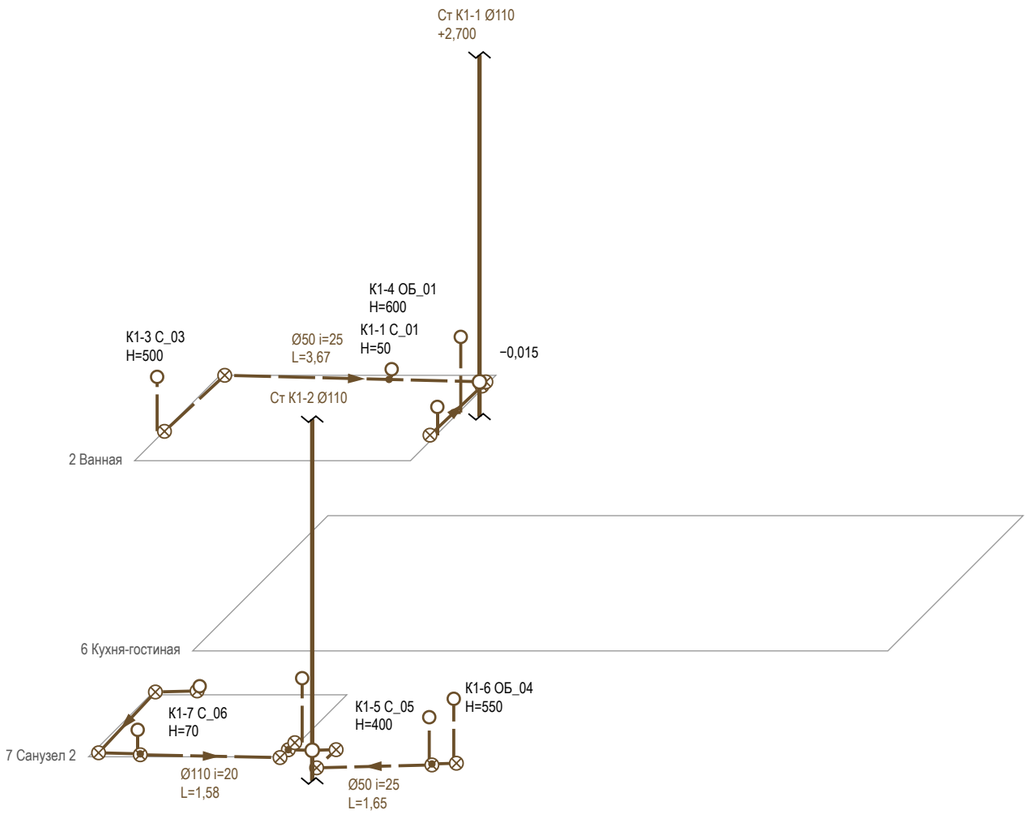

Условные обозначения


- К1 — канализация бытовая
- вывод К1 (код — в ведомости привязок)
- стояк «Ст К1-N / Ст В1-N» (ГОСТ 21.601), Ø мм
- стояк в плане (на отметке пола); вертикаль — стояк по высоте, разрыв — перекрытие
- направление уклона К1 / пола: Ø, мм на 1 м
- ревизия (прочистка) К1 — доступ сохранить
- тройник (ответвление к прибору)

Примечания


1. Схема К1 построена по тем же трассам, что план разводки: положение в плане сохранено, глубина — в масштабе ×0,5. Трассы принципиальные; фактическое положение фиксируется исполнительной схемой до закрытия.
2. Отметки — от плиты перекрытия: низ трубы у врезки в стояк — отметка из данных выпуска, к прибору труба поднимается на уклон i, мм/м (уклон не менее 1/d и не более 150 мм/м, СП 30.13330.2020, п. 19.1); чистый пол — выше плиты на стяжку (высота пирога пола). Высота выпуска прибора H — от чистого пола.
3. Ревизия — на повороте и в начале участка; стояк К1 в коробе с люком — звукоизоляция стояка в коробе; поворот — двумя отводами 45°.
4. Трубы испытать давлением до закрытия (акт скрытых работ, опрессовка по СП 73.13330.2016).
5. Диаметры, высоты выводов и места кранов — по паспортам выбранных приборов и расчёту проектной организации.
6. Расчёт систем, диаметры магистралей и подбор оборудования выполняет проектная организация.

					Проект: Трёхкомнатная квартира	М 1:50
	Лист	№ док.	Подпись	Дата		
Дизайнер	Кырлан А.С.			04.11.26	Аксонометрическая схема К1 (канализация)	Стадия: П; Лист: 21; Листов: 92

Стена А (М 1:20)

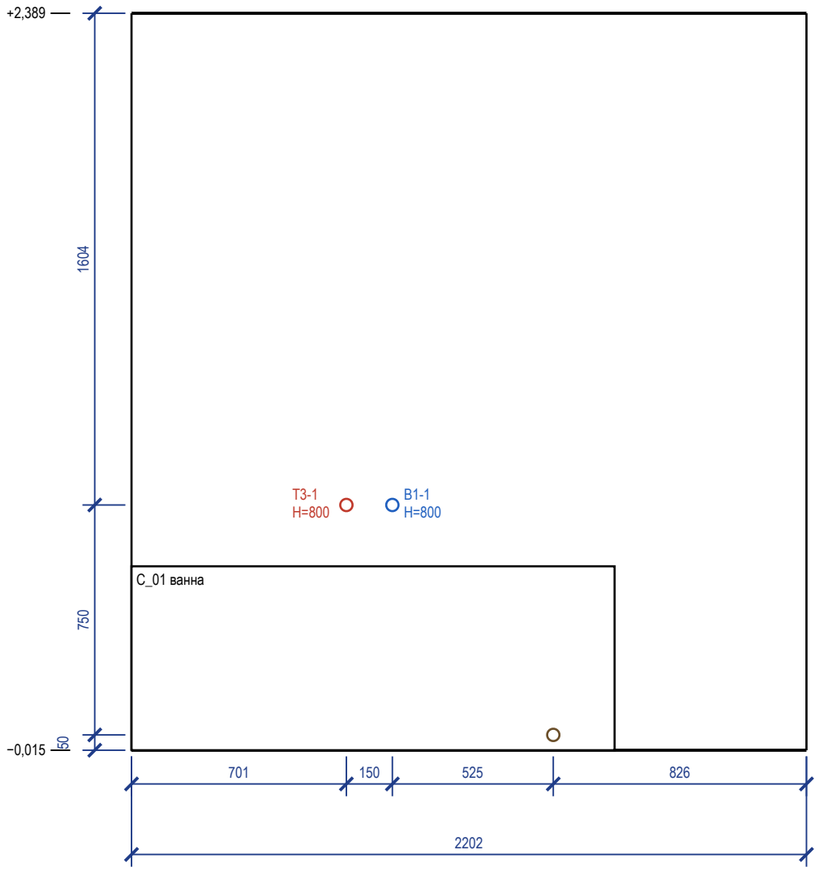

Стена Б (М 1:20)

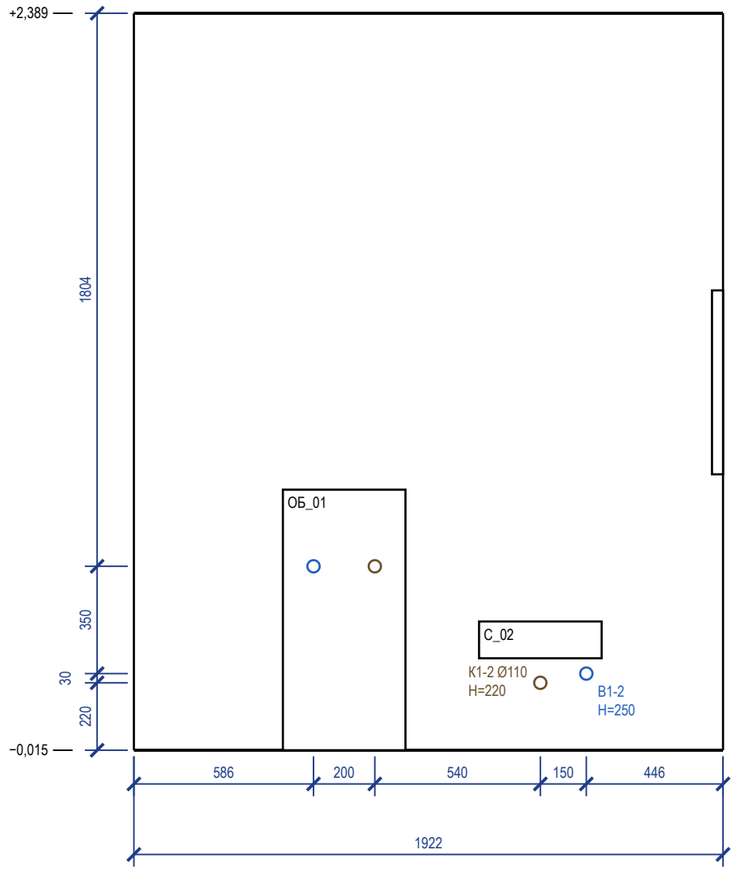

Ведомость привязок выводов (от чистого пола и угла)

Код	Прибор	Ø	H, мм	Привязка, мм
B1-1	C_01 ванна	½"	800	ст. А: 851 от лев. угла
T3-1	C_01 ванна	½"	800	ст. А: 701 от лев. угла
K1-1	C_01 ванна	Ø50	50	ст. А: 1376 от лев. угла
B1-2	C_02 унитаз подвесной	½"	250	ст. Б: 1476 от лев. угла
K1-2	C_02 унитаз подвесной	Ø110	220	ст. Б: 1326 от лев. угла
B1-4	ОБ_01 стиральная машина	½"	600	ст. Б: 586 от лев. угла
K1-4	ОБ_01 стиральная машина	Ø50	600	ст. Б: 786 от лев. угла

Условные обозначения


- вывод B1 (код — в ведомости привязок)
- вывод T3 (код — в ведомости привязок)
- вывод K1 (код — в ведомости привязок)
- сантехприбор по расстановке (габарит модели)
- дверной проём; окно — сплошной контур

Примечания


1. Габариты и высоты приборов, межосевые смесителей и места кранов — по паспортам выбранных приборов, сверяются до разметки стен.
2. Высоты H — от чистого пола помещения, мм; отметка чистого пола и потолка — у левого края вида (от ±0,000 объекта). Привязки — от левого чистового угла вида (облицовка стен вычтена), как на развёртках стен.
3. Стояки в помещении: Ст К1-1 Ø110, Ст В1-1 Ø32, Ст Т3-1 Ø32 — положение на плане выводов; выводы подключаются к ним по схеме разводки.
4. Ревизионные люки (стояки Ст К1-1, Ст В1-1 (короб Ш1) 300×400): место в стене на развёртке не задано (записи реестра нет).
5. Часть подписей выводов не уместилась у знака: коды и высоты — в ведомости привязок.
6. Помещение «Ванная» — 2 листа: стены 1) А, Б; 2) В, Г.
7. Расчёт систем водоснабжения и канализации и подбор оборудования выполняет проектная организация; лист задаёт места и высоты выводов.

					Проект: Трёхкомнатная квартира	М 1:20
	Лист	№ док.	Подпись	Дата		
Дизайнер	Кырлан А.С.			04.11.26	Развёртки мокрых зон: выводы ВК. Ванная (лист 1 из 2)	Стадия: П; Лист: 22; Листов: 92

Стена В (М 1:20)

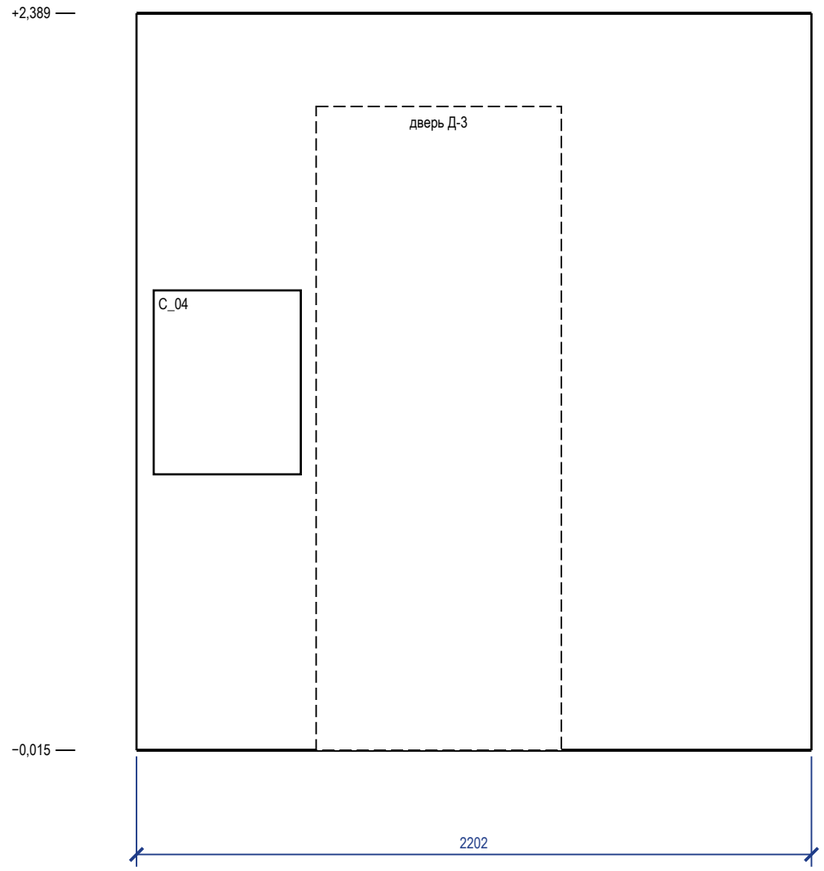

Стена Г (М 1:20)

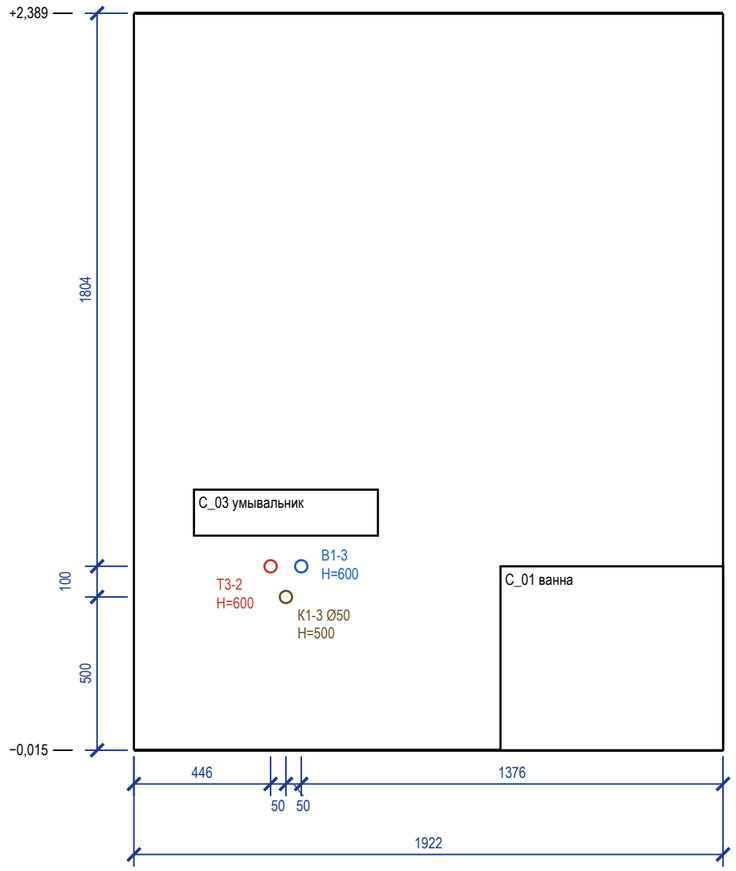

Ведомость привязок выводов (от чистого пола и угла)

Код	Прибор	Ø	H, мм	Привязка, мм
B1-3	С_03 умывальник	½"	600	ст. Г: 546 от лев. угла
T3-2	С_03 умывальник	½"	600	ст. Г: 446 от лев. угла
K1-3	С_03 умывальник	Ø50	500	ст. Г: 496 от лев. угла

Условные обозначения


- вывод B1 (код — в ведомости привязок)
- вывод T3 (код — в ведомости привязок)
- вывод K1 (код — в ведомости привязок)
- сантехприбор по расстановке (габарит модели)
- дверной проём; окно — сплошной контур

Примечания

1. Габариты и высоты приборов, межосевые смесителей и места кранов — по паспортам выбранных приборов, сверяются до разметки стен.
2. Высоты H — от чистого пола помещения, мм; отметка чистого пола и потолка — у левого края вида (от ±0,000 объекта). Привязки — от левого чистового угла вида (облицовка стен вычтена), как на развёртках стен.
3. Стояки в помещении: Ст К1-1 Ø110, Ст В1-1 Ø32, Ст Т3-1 Ø32 — положение на плане выводов; выводы подключаются к ним по схеме разводки.
4. Ревизионные люки (стояки Ст К1-1, Ст В1-1 (короб Ш1) 300×400): место в стене на развёртке не задано (записи реестра нет).
5. Помещение «Ванная» — 2 листа: стены 1) А, Б; 2) В, Г.
6. Расчёт систем водоснабжения и канализации и подбор оборудования выполняет проектная организация; лист задаёт места и высоты выводов.

					Проект: Трёхкомнатная квартира	М 1:20
	Лист	№ док.	Подпись	Дата		
Дизайнер	Кырлан А.С.			04.11.26	Развёртки мокрых зон: выводы ВК. Ванная (лист 2 из 2)	Стадия: П; Лист: 23; Листов: 92

Стена В (М 1:20)

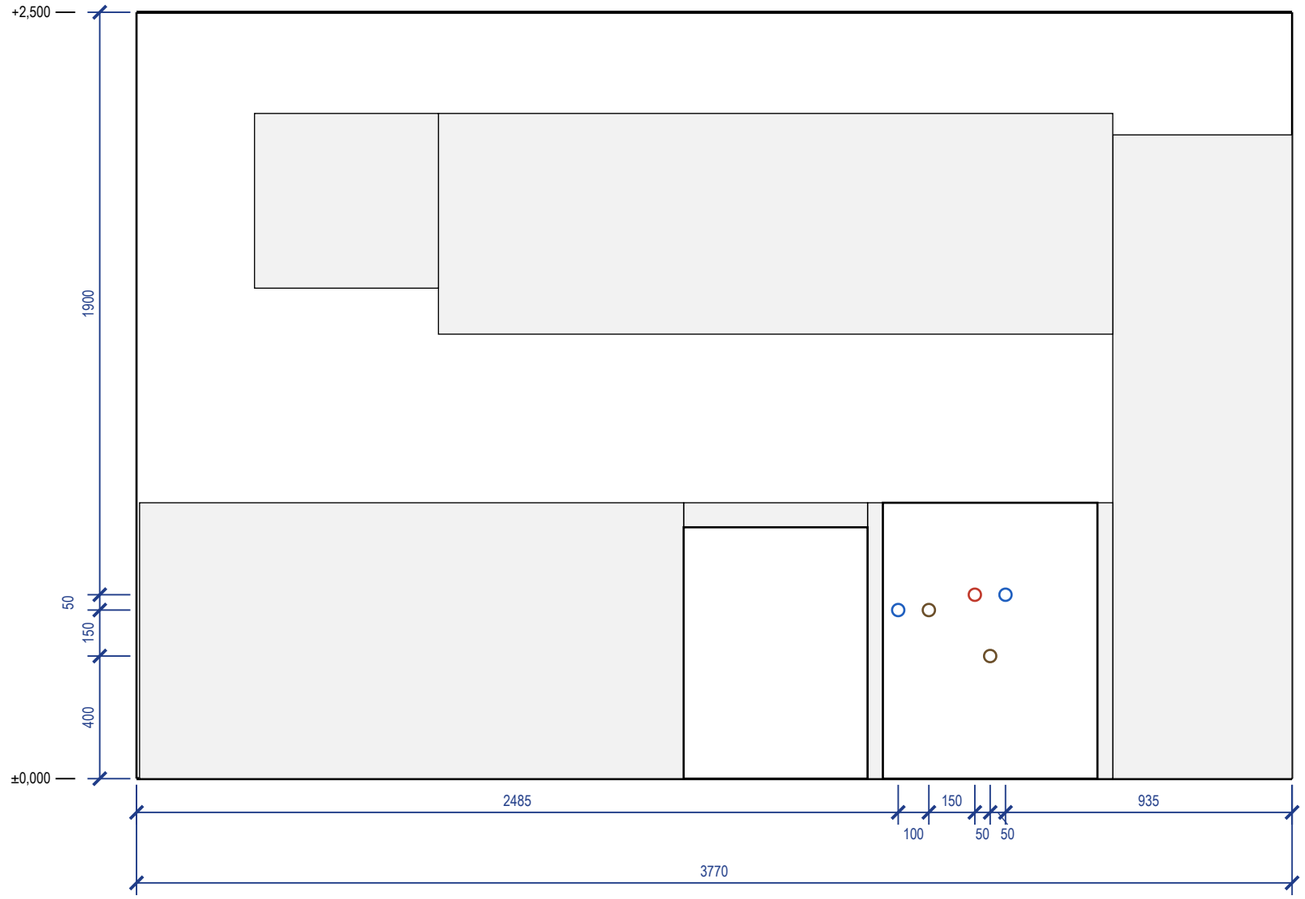

Ведомость привязок выводов (от чистого пола и угла)

Код	Прибор	Ø	H, мм	Привязка, мм
В1-5	С_05 мойка кухонная	½"	600	ст. В: 2835 от лев. угла
Т3-3	С_05 мойка кухонная	½"	600	ст. В: 2735 от лев. угла
К1-5	С_05 мойка кухонная	Ø50	400	ст. В: 2785 от лев. угла
В1-6	ОБ_04 посудомоечная машина	½"	550	ст. В: 2485 от лев. угла
К1-6	ОБ_04 посудомоечная машина	Ø40	550	ст. В: 2585 от лев. угла

Условные обозначения


- вывод В1 (код — в ведомости привязок)
- вывод Т3 (код — в ведомости привязок)
- вывод К1 (код — в ведомости привязок)
- сантехприбор по расстановке (габарит модели)
- дверной проём; окно — сплошной контур

Примечания


1. Габариты и высоты приборов, межосевые смесителей и места кранов — по паспортам выбранных приборов, сверяются до разметки стен.
2. Высоты Н — от чистого пола помещения, мм; отметка чистого пола и потолка — у левого края вида (от ±0,000 объекта). Привязки — от левого чистового угла вида (облицовка стен вычтена), как на развёртках стен.
3. Ревизионные люки к арматуре и ревизиям в данных не заданы: место и размер не определены (записи реестра нет).
4. Мойка, ПММ и фильтр — выводы в шкафу мойки; диаметры и положение сифона и кранов сверить по паспортам приборов и чертежам модуля.
5. Часть подписей выводов не уместилась у знака: коды и высоты — в ведомости привязок.
6. Расчёт систем водоснабжения и канализации и подбор оборудования выполняет проектная организация; лист задаёт места и высоты выводов.

					Проект: Трёхкомнатная квартира	М 1:20
	Лист	№ док.	Подпись	Дата		
Дизайнер	Кырлан А.С.			04.11.26	Развёртки мокрых зон: выводы ВК. Кухня-гостиная	Стадия: П; Лист: 24; Листов: 92


Стена А (М 1:25)

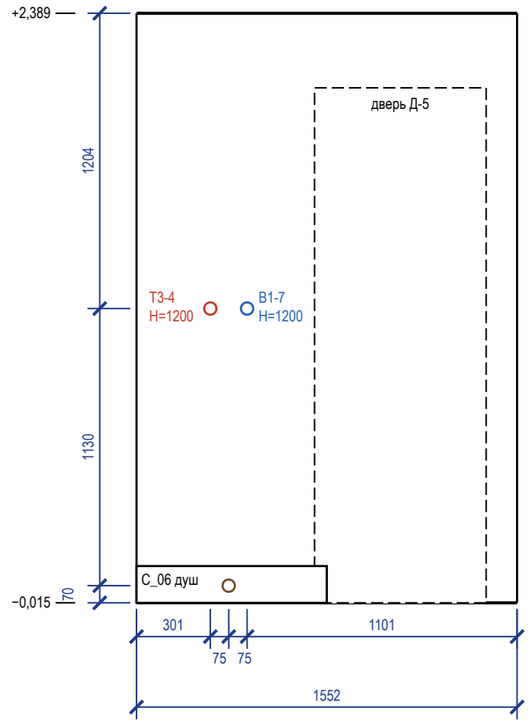


Стена Б (М 1:25)

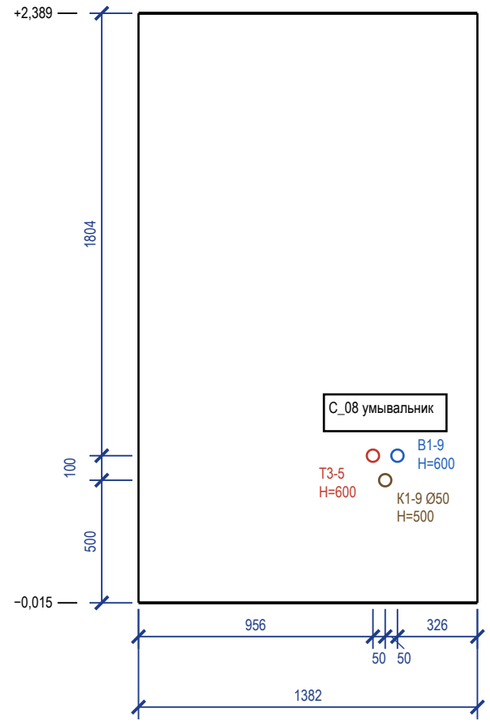

Стена В (М 1:25)

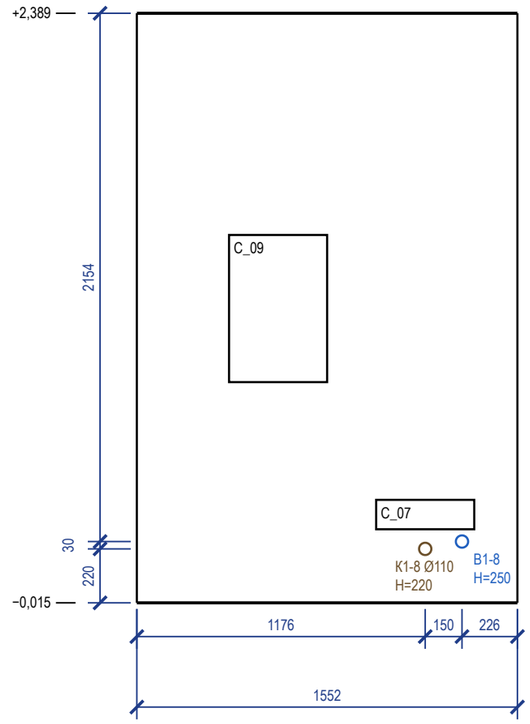

Стена Г (М 1:25)

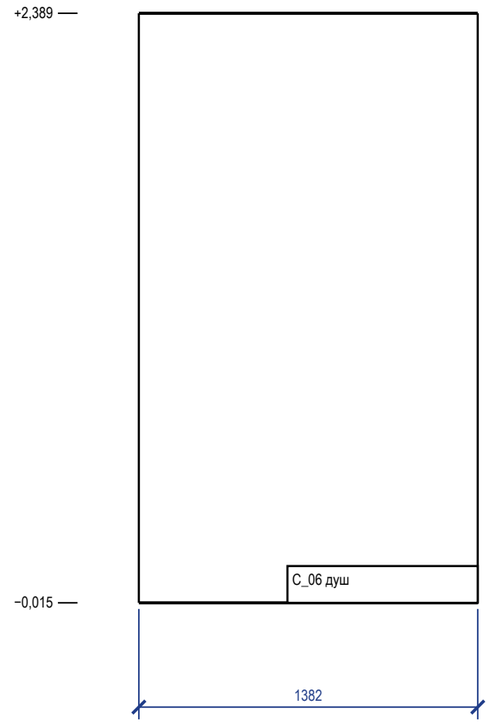

Ведомость привязок выводов (от чистого пола и угла)

Код	Прибор	Ø	H, мм	Привязка, мм
B1-7	C_06 душ	½"	1200	ст. А: 451 от лев. угла
T3-4	C_06 душ	½"	1200	ст. А: 301 от лев. угла
K1-7	C_06 душ	Ø50	70	ст. А: 376 от лев. угла
B1-9	C_08 умывальник	½"	600	ст. Б: 1056 от лев. угла
T3-5	C_08 умывальник	½"	600	ст. Б: 956 от лев. угла
K1-9	C_08 умывальник	Ø50	500	ст. Б: 1006 от лев. угла
B1-8	C_07 унитаз подвесной	½"	250	ст. В: 1326 от лев. угла
K1-8	C_07 унитаз подвесной	Ø110	220	ст. В: 1176 от лев. угла

Условные обозначения

- вывод B1 (код — в ведомости привязок)
- вывод T3 (код — в ведомости привязок)
- вывод K1 (код — в ведомости привязок)
- сантехприбор по расстановке (габарит модели)
- дверной проём; окно — сплошной контур

Примечания

1. Габариты и высоты приборов, межосевые смесителей и места кранов — по паспортам выбранных приборов, сверяются до разметки стен.
2. Высоты H — от чистого пола помещения, мм; отметка чистого пола и потолка — у левого края вида (от ±0,000 объекта). Привязки — от левого чистового угла вида (облицовка стен вычтена), как на развёртках стен.
3. Стояки в помещении: Ст Т3-2 Ø32 — положение на плане выводов; выводы подключаются к ним по схеме разводки.
4. Ревизионные люки (стояки Ст К1-2, Ст В1-2 (шахта Ш2) 300×400): место в стене на развёртке не задано (записи реестра нет).
5. Часть подписей выводов не уместилась у знака: коды и высоты — в ведомости привязок.
6. Расчёт систем водоснабжения и канализации и подбор оборудования выполняет проектная организация; лист задаёт места и высоты выводов.

					Проект: Трёхкомнатная квартира	М 1:25
	Лист	№ док.	Подпись	Дата		
Дизайнер	Кырлан А.С.			04.11.26	Развёртки мокрых зон: выводы ВК. Санузел 2	Стадия: П; Лист: 25; Листов: 92


Поз.	Наименование и техническая характеристика	Тип, марка, обозначение документа	Код продукции	Поставщик	Ед. изм.	Кол.	Масса 1 ед., кг	Примечание
	Санитарные приборы							
1	Ванна встраиваемая акриловая 1600×750 мм, с каркасом, экраном и отверстием слив-перелив	аналог		выбор заказчика	шт	1		С_01
2	Унитаз подвесной безободковый, с сиденьем микролифт, крепёж и звукоизолирующая прокладка	аналог		выбор заказчика	шт	2		С_02, С_07
3	Инсталляция для подвесного унитаза: рама высотой 1120 мм, бачок, клавиша смыва (ось клавиши 1050 мм от чистого пола)	аналог		выбор заказчика	шт	2		С_02, С_07; короб ГКЛВ
4	Умывальник подвесной 450×600 мм, с отверстием под смеситель и переливом	аналог		выбор заказчика	шт	1		С_03
5	Умывальник подвесной 350×500 мм, с отверстием под смеситель и переливом	аналог		выбор заказчика	шт	1		С_08
6	Поддон душевой низкий 800×800 мм, с сифоном и выпуском Ø50, на ножках/подиуме	аналог		выбор заказчика	шт	1		С_06
7	Мойка кухонная врезная 700×480 мм, с переливом	аналог		с кухонной мебелью	шт	1		С_05
8	Полотенцесушитель электрический, IP44, с терморегулятором	аналог		выбор заказчика	шт	2		С_04, С_09
	Смесители, сифоны и арматура приборов							
9	Смеситель для ванны настенный однорычажный, межосевое 150 мм, с душевым набором (лейка, шланг, держатель)	аналог		выбор заказчика	шт	1		С_01
10	Смеситель для умывальника однорычажный, с донным клапаном	аналог		выбор заказчика	шт	2		С_03, С_08
11	Душевая система скрытого монтажа с термостатом: встраиваемая часть, верхний душ, ручная лейка	аналог		выбор заказчика	шт	1		С_06; встраиваемая часть — до плитки
12	Смеситель кухонный однорычажный, высокий излив	аналог		выбор заказчика	шт	1		С_05
13	Обвязка ванны слив-перелив Ø40/50 с сифоном	аналог		выбор заказчика	шт	1		С_01
14	Сифон для умывальника бутылочный Ø32/40–50, с гофрой к выпуску	аналог		выбор заказчика	шт	2		С_03, С_08
15	Сифон для мойки Ø40/50	аналог		выбор заказчика	шт	1		С_05
16	Сифон для посудомоечной машины с обратным клапаном, на выводе слива Ø40	аналог		выбор заказчика	шт	1		ОБ_04
17	Сифон для стиральной машины встраиваемый в стену Ø50, с обратным клапаном	аналог		выбор заказчика	шт	1		ОБ_01
18	Кран угловой ½"×½" с гибкой подводкой 40 см (умывальники, мойка)	аналог		выбор заказчика	шт	6		по 2 на прибор
19	Кран шаровой угловой ½"×¾" для подключения стиральной и посудомоечной машины	аналог		выбор заказчика	шт	2		ОБ_01, ОБ_04
	Трубопроводы							
20	Труба полипропиленовая PP-R PN20 Ø20×3,4 (В1)	ГОСТ 32415-2013		выбор заказчика	м	18,5	0,17	11,2 + 5,5 + 10 %
21	Труба PP-R, армированная стекловолокном, PN20 Ø20×2,8 (Т3)	ГОСТ 32415-2013		выбор заказчика	м	13,5	0,15	8,2 + 3,8 + 10 %
22	Труба канализационная ПП Ø40 (К1)	ГОСТ 32414-2013		выбор заказчика	м	1		0,3 + 0,6 + 10 %
23	Труба канализационная ПП Ø50 (К1)	ГОСТ 32414-2013		выбор заказчика	м	11		7,7 + 2,1 + 10 %
24	Труба канализационная ПП Ø110 (К1)	ГОСТ 32414-2013		выбор заказчика	м	4		2,9 + 0,4 + 10 %
	Фасонные части и выводы							
25	Отвод канализационный ПП 45° Ø40	ГОСТ 32414-2013		выбор заказчика	шт	2		2 шт. на поворот
26	Отвод канализационный ПП 45° Ø50	ГОСТ 32414-2013		выбор заказчика	шт	20		2 шт. на поворот
27	Отвод канализационный ПП 45° Ø110	ГОСТ 32414-2013		выбор заказчика	шт	10		2 шт. на поворот
28	Тройник канализационный ПП 45° (врезки ветвей)	ГОСТ 32414-2013		выбор заказчика	шт	8		
29	Ревизия канализационная ПП (после поворота трассы)	ГОСТ 32414-2013		выбор заказчика	шт	9		доступ сохранить
30	Фитинги PP-R Ø20: тройники, угольники 90° (ветви и повороты В1, Т3)	ГОСТ 32415-2013		выбор заказчика	шт	34		
31	Водорозетка PP-R Ø20×½" настенная, с креплением	ГОСТ 32415-2013		выбор заказчика	шт	14		коды — лист выводов
	Узлы ввода, люки, короба							
32	Кран шаровой латунный Ду15 PN16 (отключение ввода)	аналог		выбор заказчика	шт	4		Ст В1-1, Ст В1-2, Ст Т3-1, Ст Т3-2
33	Фильтр сетчатый косой Ду15	аналог		выбор заказчика	шт	4		
34	Счётчик воды крыльчатый Ду15 (ХВ, ГВ), с поверкой	аналог		выбор заказчика	шт	4		пломба УК
35	Клапан обратный Ду15	аналог		выбор заказчика	шт	4		
36	Люк ревизионный нажимной под плитку 300×400 мм	аналог		выбор заказчика	шт	2		к стоякам и арматуре
37	Звукоизоляция стояка К1 в коробе: рулонный звукоизоляционный материал ≥ 10 мм, обмотка стояка на высоту этажа	аналог		выбор заказчика	м	5,4		Ст К1-1, Ст К1-2
38	Короб К1 над полом: профиль ПН/ПС, ГКЛВ 12,5 мм под плитку	аналог		выбор заказчика	м	2,4		сечение — лист разводки

Примечания

1. Форма 1 ГОСТ 21.110-2013, ширины граф изменены по п. 4.1. «Аналог» — аналог по характеристикам: модели внести до черновых работ, привязки выводов сверить по паспортам.
2. Бытовая техника не входит (показана арматура подключения), мойка — в комплекте кухни (марка — модуля кухни, как у столяра). Длины труб — трасса листа разводки + подъёмы + 10 %.
3. Стояк К1 в коробе — звукоизоляция стояка в коробе без жёсткого контакта короба с трубой.
4. Расчёт систем водоснабжения и канализации, диаметры магистралей и подбор оборудования выполняет проектная организация.

					Проект: Трёхкомнатная квартира
	Лист	№ док.	Подпись	Дата	
Дизайнер	Кырлан А.С.			04.11.26	Спецификация сантехнического оборудования

Стадия	Лист	Листов
П	26	92

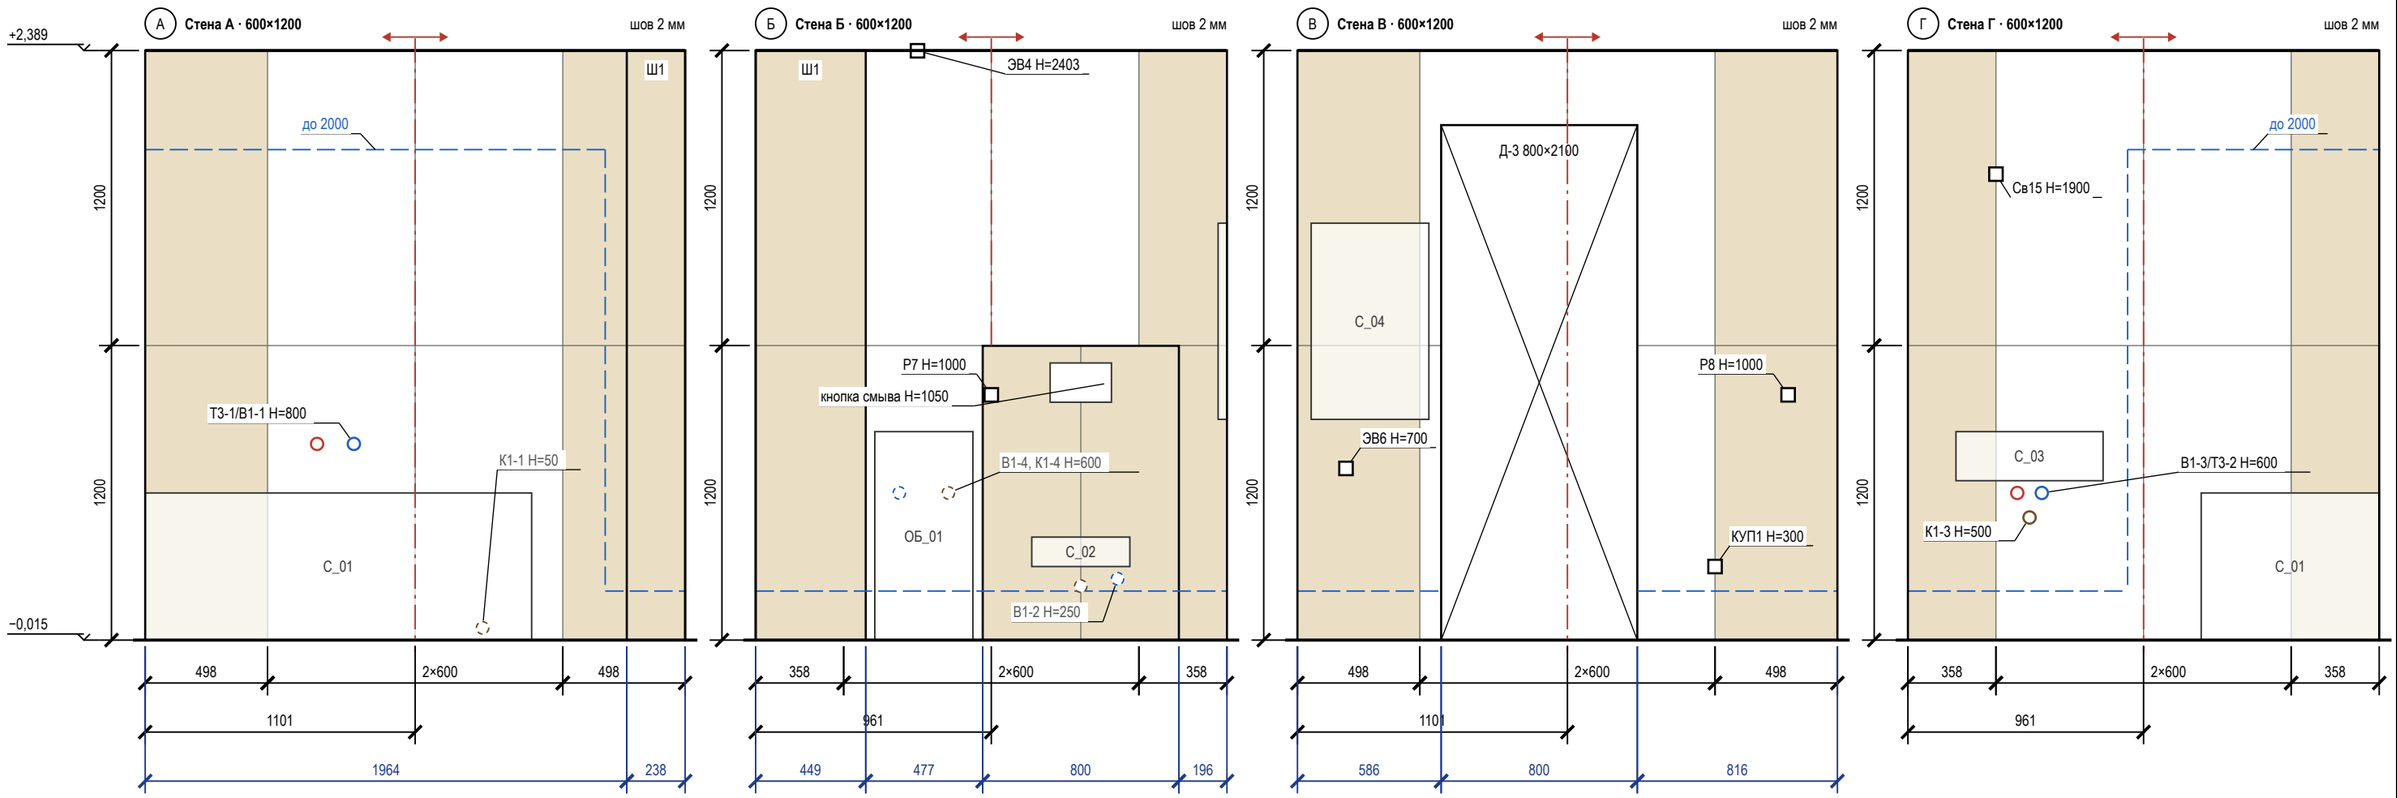

Подсчёт плитки по стенам и коробу

Поверхность	L × H, мм	S, м²	Целых	Подр.	С запасом	Подрезки: край / верх, мм
стена А	2202 × 2404	4,84	4	4	9	498 / 498; целый ряд
Ш1 248×459, ст. А	238 × 2404	0,57	0	2	3	лицо 238
стена Б	1922 × 2404	2,70	1	4	6	358 / 358; целый ряд
Ш1 248×459, ст. Б	449 × 2404	1,08	0	2	3	лицо 449
короб (ст. Б)	800×1200×250	1,76	0	6	7	лицо 399 / 399; бок. 250
стена В	2202 × 2404	3,73	0	8	9	498 / 498; целый ряд
стена Г	1922 × 2404	4,74	4	4	9	358 / 358; целый ряд
Итого		**19,41**	**9**	**30**	**46**	


Условные обозначения

- плитка целая; тонкая линия — шов
- плитка с подрезкой (размер — на цепочке)
- ось старта; стрелки — направление укладки
- верх гидроизоляции: 200 от ЧП, в мокрой зоне — «до …»
- проём — не облицовывается
- сантехприбор: габарит, высота по практике
- короб инсталляции, в нём кнопка смыва 250×160
- грань короба стояков (Ш…): своя сетка, за коробом плитку не кладут
- вывод В1 (код — в ведомости привязок)
- вывод Т3 (код — в ведомости привязок)
- вывод К1 (код — в ведомости привязок)
- вывод за прибором / в коробе (не на сетке)
- электроточка: марка и Н — по листам ЭОМ
- отметка уровня, м: ±0,000 — чистый пол жилых помещений
- низ потолка; серая полоса — стена без плитки
- А — обозначение стены А–Г (как на развёртках)

Примечания

1. Вид изнутри, стены по часовой стрелке А → Г. Высоты — от чистого пола (−0,015), отметки — от ±0,000. Раскладка от чистовых размеров (штукатурка 10 + клей 5 + плитка 9 мм), подрезки чистые; старт — от оси стены, ряды от пола целыми.
2. Облицовка до потолка (+2,389).
3. Открытые выводы и электроточки — на шве или в центре плитки (допуск 10 мм; плитка от 900 мм по высоте — на шве или не ближе 60 мм к нему).
4. Выводы ВК стоят по оси прибора и с прибором не двигаются — привязки по «Плану выводов сантехники» без сдвига; вне сетки (Т3-1/В1-1, В1-3/Т3-2, К1-3) отверстие в плитке коронкой по той же привязке, плитку не сдвигать.
5. За приборами и в коробе (К1-1, В1-2, К1-2, В1-4, К1-4) — штриховым кольцом.
6. Гидроизоляция: 200 мм от ЧП по периметру; над ванной — до 2000 и 300 мм за борт (СП 29.13330.2011, п. 7.2 — на высоту замачивания); углы — лентой; акт скрытых работ, пролив.
7. Короб 800×1200×250: лицо 399 / 399 мм от оси кнопки смыва, боковины, полка; углы — запил 45° или профиль; за коробом плитку не кладут.
8. Между коробом и углом полоса 196 мм — довести короб до угла.
9. Короб стояков Ш1: грани 238 мм (ст. А), 449 мм (ст. Б) — плиткой стен по рядам стены, целая плитка от наружного угла; угол — запил 45° или профиль; за коробом плитку не кладут. Люк 300×400 — на грани ст. Б: высота — по месту ревизии стояка (положение стояков сверяется на объекте), кромки дверцы по швам сетки, дверца нажимная под плитку.

					Проект: Трёхкомнатная квартира — **М 1:25**
	Лист	№ док.	Подпись	Дата	Раскладка плитки. Ванная. Развёртки стен
Дизайнер	Кырлан А.С.			04.11.26	Стадия: П · Лист: 27 · Листов: 92

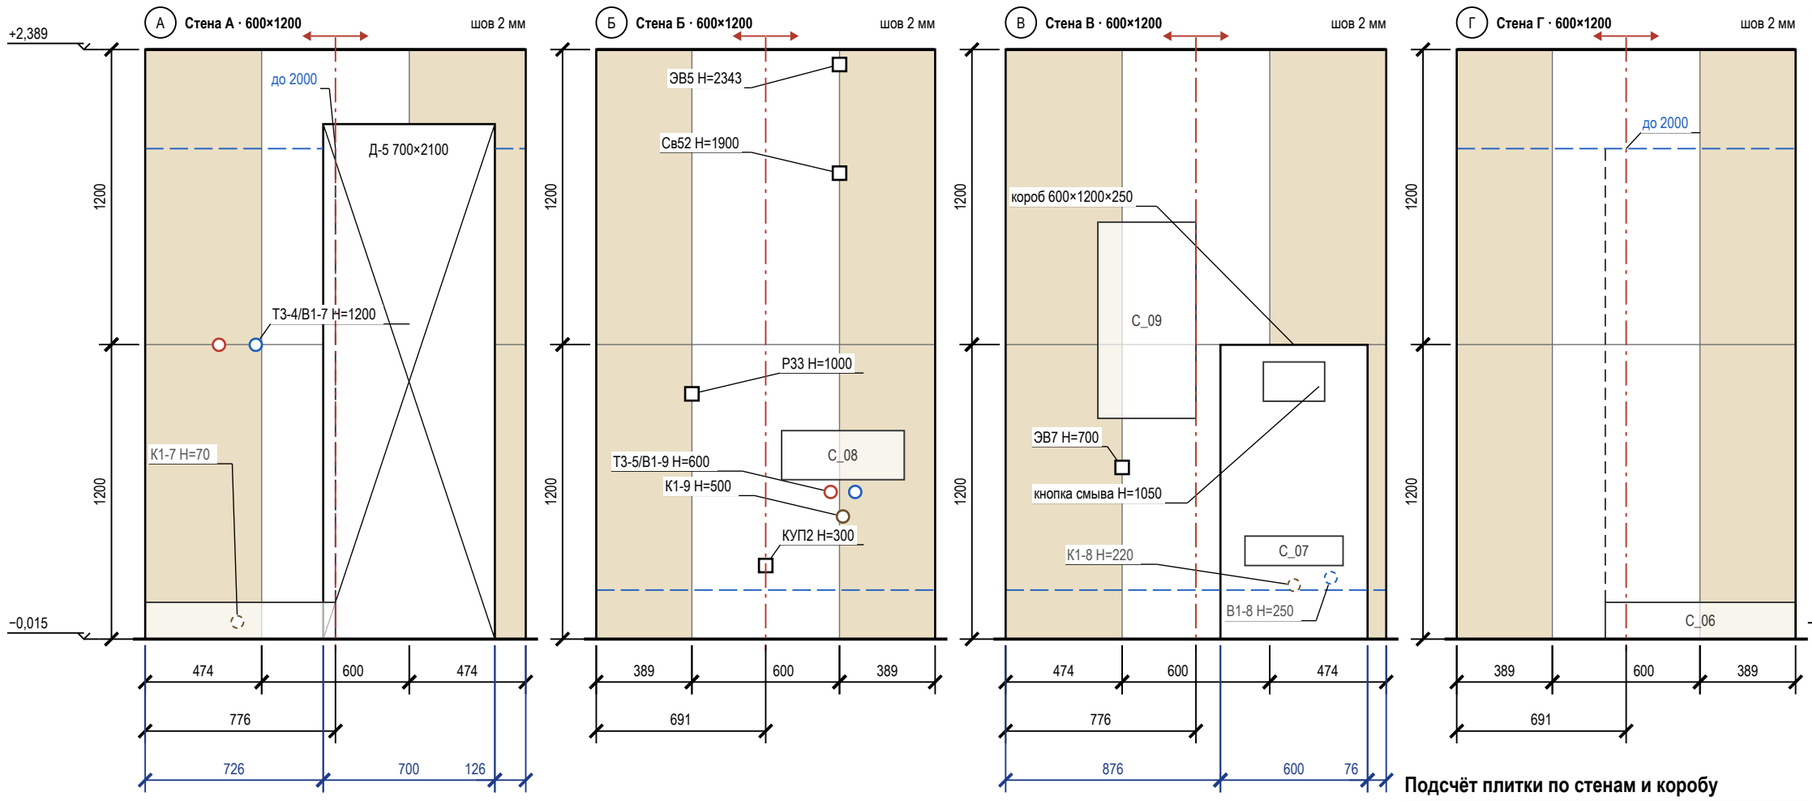

Условные обозначения

- плитка целая; тонкая линия — шов
- плитка с подрезкой (размер — на цепочке)
- ось старта; стрелки — направление укладки
- верх гидроизоляции: 200 от ЧП, в мокрой зоне — «до …»
- проём — не облицовывается
- сантехприбор: габарит, высота по практике
- граница душевой зоны (ограждение)
- короб инсталляции, в нём кнопка смыва 250×160
- вывод В1 (код — в ведомости привязок)
- вывод Т3 (код — в ведомости привязок)
- вывод К1 (код — в ведомости привязок)
- вывод за прибором / в коробе (не на сетке)
- электроточка: марка и Н — по листам ЭОМ
- отметка уровня, м: ±0,000 — чистый пол жилых помещений
- низ потолка; серая полоса — стена без плитки
- А — обозначение стены А–Г (как на развёртках)

Подсчёт плитки по стенам и коробу

Поверхность	L × H, мм	S, м²	Целых	Подр.	С запасом	Подрезки: край / верх, мм
стена А	1552 × 2404	2,38	0	6	7	474 / 474; целый ряд
стена Б	1382 × 2404	3,44	2	4	7	389 / 389; целый ряд
стена В	1552 × 2404	3,13	1	5	7	474 / 474; целый ряд
короб (ст. В)	600×1200×250	1,47	1	3	5	лицо 600; бок. 250
стена Г	1382 × 2404	3,44	2	4	7	389 / 389; целый ряд
Итого		**13,85**	**6**	**22**	**33**	

Примечания

1. Вид изнутри, стены по часовой стрелке А → Г. Высоты — от чистого пола (−0,015), отметки — от ±0,000. Раскладка от чистовых размеров (штукатурка 10 + клей 5 + плитка 9 мм), подрезки чистые; старт — от оси стены, ряды от пола целыми.
2. Облицовка до потолка (+2,389).
3. Открытые выводы и электроточки — на шве или в центре плитки (допуск 10 мм; плитка от 900 мм по высоте — на шве или не ближе 60 мм к нему).
4. Выводы ВК стоят по оси прибора и с прибором не двигаются — привязки по «Плану выводов сантехники» без сдвига; вне сетки (Т3-4/В1-7, Т3-5/В1-9, К1-9) — отверстие в плитке коронкой по той же привязке, плитку не сдвигать.
5. За приборами и в коробе (К1-7, В1-8, К1-8) — штриховым кольцом.
6. Гидроизоляция: 200 мм от ЧП по периметру; у душа — до 2000 и 500 мм за поддон (СП 29.13330.2011, п. 7.2 — на высоту замачивания); углы — лентой; акт скрытых работ, пролив.
7. Короб 600×1200×250: лицо 600 мм от оси кнопки смыва, боковины, полка; углы — запил 45° или профиль; за коробом плитку не кладут.
8. Между коробом и углом полоса 76 мм — довести короб до угла.


	Лист	№ док.	Подпись	Дата
Дизайнер	Кырлан А.С.			04.11.26

Проект: Трёхкомнатная квартира — **М 1:25**

Раскладка плитки. Санузел 2. Развёртки стен

Стадия	Лист	Листов
П	28	92

выпуск 04.11.2026 № 503a52061a · стр. 28 из 92

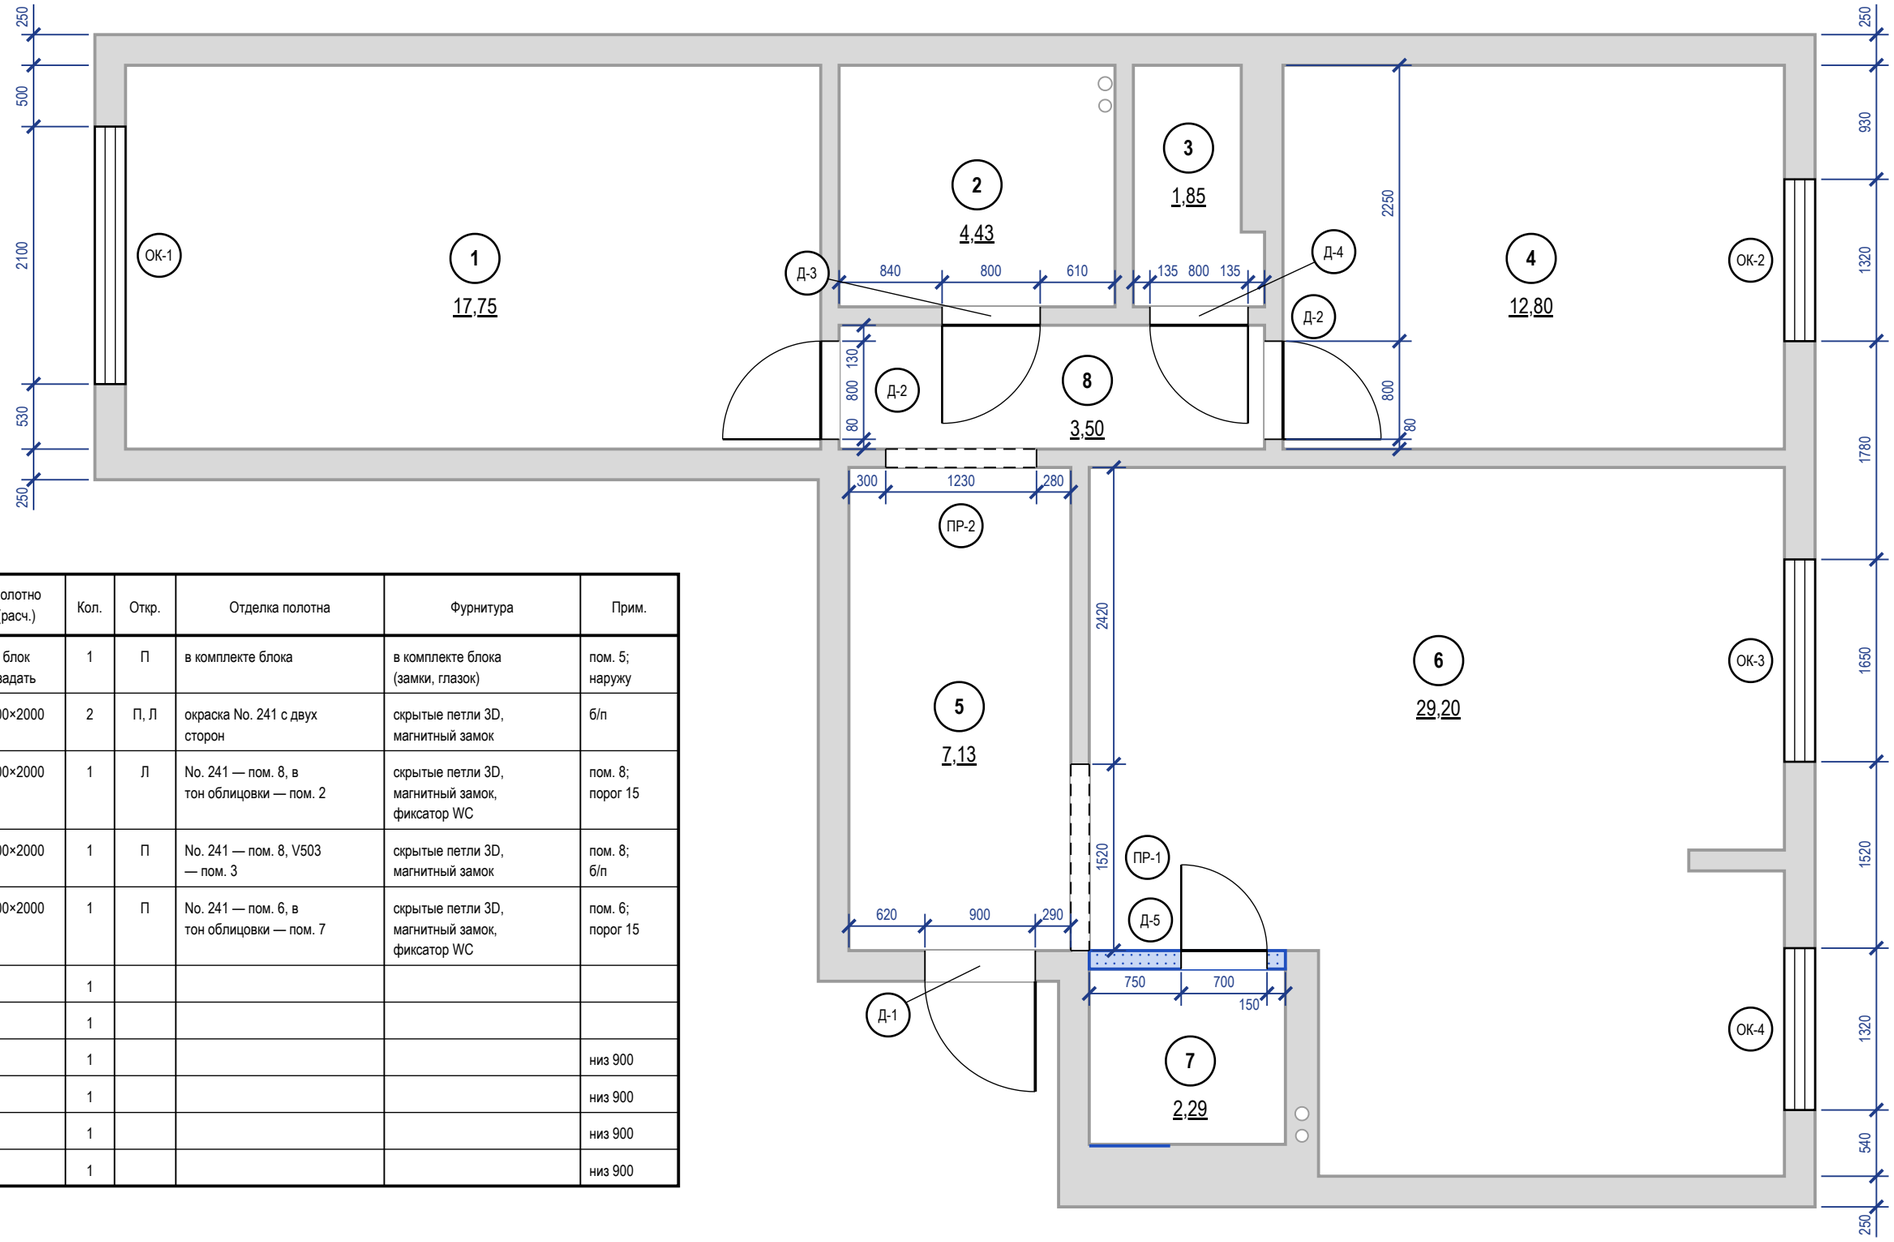


Ведомость заполнения проёмов

Марка	Наименование, обозначение	Проём ш×в, мм	Полотно (расч.)	Кол.	Откр.	Отделка полотна	Фурнитура	Прим.
Д-1	Блок дверной входной, ГОСТ 31173-2016	900×2100	блок задать	1	П	в комплекте блока	в комплекте блока (замки, глазок)	пом. 5; наружу
Д-2	Дверь скрытого монтажа, ТУ изготовителя	800×2100	700×2000	2	П, Л	окраска No. 241 с двух сторон	скрытые петли 3D, магнитный замок	б/п
Д-3	Дверь скрытого монтажа, ТУ изготовителя	800×2100	700×2000	1	Л	No. 241 — пом. 8, в тон облицовки — пом. 2	скрытые петли 3D, магнитный замок, фиксатор WC	пом. 8; порог 15
Д-4	Дверь скрытого монтажа, ТУ изготовителя	800×2100	700×2000	1	П	No. 241 — пом. 8, V503 — пом. 3	скрытые петли 3D, магнитный замок	пом. 8; б/п
Д-5	Дверь скрытого монтажа, ТУ изготовителя	700×2100	600×2000	1	П	No. 241 — пом. 6, в тон облицовки — пом. 7	скрытые петли 3D, магнитный замок, фиксатор WC	пом. 6; порог 15
ПР-1	Портал без заполнения	1520×2500		1				
ПР-2	Портал без заполнения	1230×2100		1				
ОК-1	Блок оконный существующий	2100×1500		1				низ 900
ОК-2	Блок оконный существующий	1320×1500		1				низ 900
ОК-3	Блок оконный существующий	1650×1500		1				низ 900
ОК-4	Блок оконный существующий	1320×1400		1				низ 900

Примечания

1. Размеры проёмов и привязки — в миллиметрах от чистых граней стен до отделки; привязка — от угла того помещения, со стороны которого стоит размер. Размер проёма — ширина × высота от чистого пола 0,000. Размеры на плане — проёмов, не полотен: полотно — в ведомости, коробка — по системе. Откос от угла помещения до проёма с коробкой — не менее 50 мм.
2. Марки в кружках — типы заполнения проёмов (ГОСТ 21.501-2018, п. 5.3.2); одна марка — один типоразмер; количество сверено с планом.
3. Открывание: Л — петли слева, П — справа, если смотреть со стороны, куда открывается полотно (на себя).
4. Скрытые двери (Д-2…Д-5): проём замерить в чистоте; блок заказать до штукатурки (≈ 30 дн.), короб ставить до штукатурки; полотно навесить после чистовой отделки, красить в цвет стен. Порядок — практика монтажа, изготовитель подтверждает.
5. Д-2…Д-4 — существующие проёмы, до техзаключения не расширять. Д-3, Д-4: стена принята 150 мм, по скану 85 мм, не замерено; узел — для 150 мм.
6. Полотно «расч.» — по проёму с запасом по каталогам, заказ — по таблице проёмов модели; Д-2…Д-5: проём 2100, а под полотно 2000 по каталогам нужен 2050–2080, под 2100 — 2150–2180: высоту проёма — по модели; Д-1: входной блок по ГОСТ 31173-2016 — задать при выборе блока.
7. Окна ОК-1…ОК-4 существующие, сохраняются; подоконники и откосы не заданы — приняты.
8. Размеры проёмов и привязки сняты со скана плана заказчика и на объекте не замерены (обмерный план — лист 5).
9. Экспликация помещений — лист 5; в марках помещений — номер и площадь, м².

					Проект: Трёхкомнатная квартира	**М 1:50**
	Лист	№ док.	Подпись	Дата		
Дизайнер	Кырлан А.С.			04.11.26	План размещения дверей	Стадия: П; Лист: 29; Листов: 92

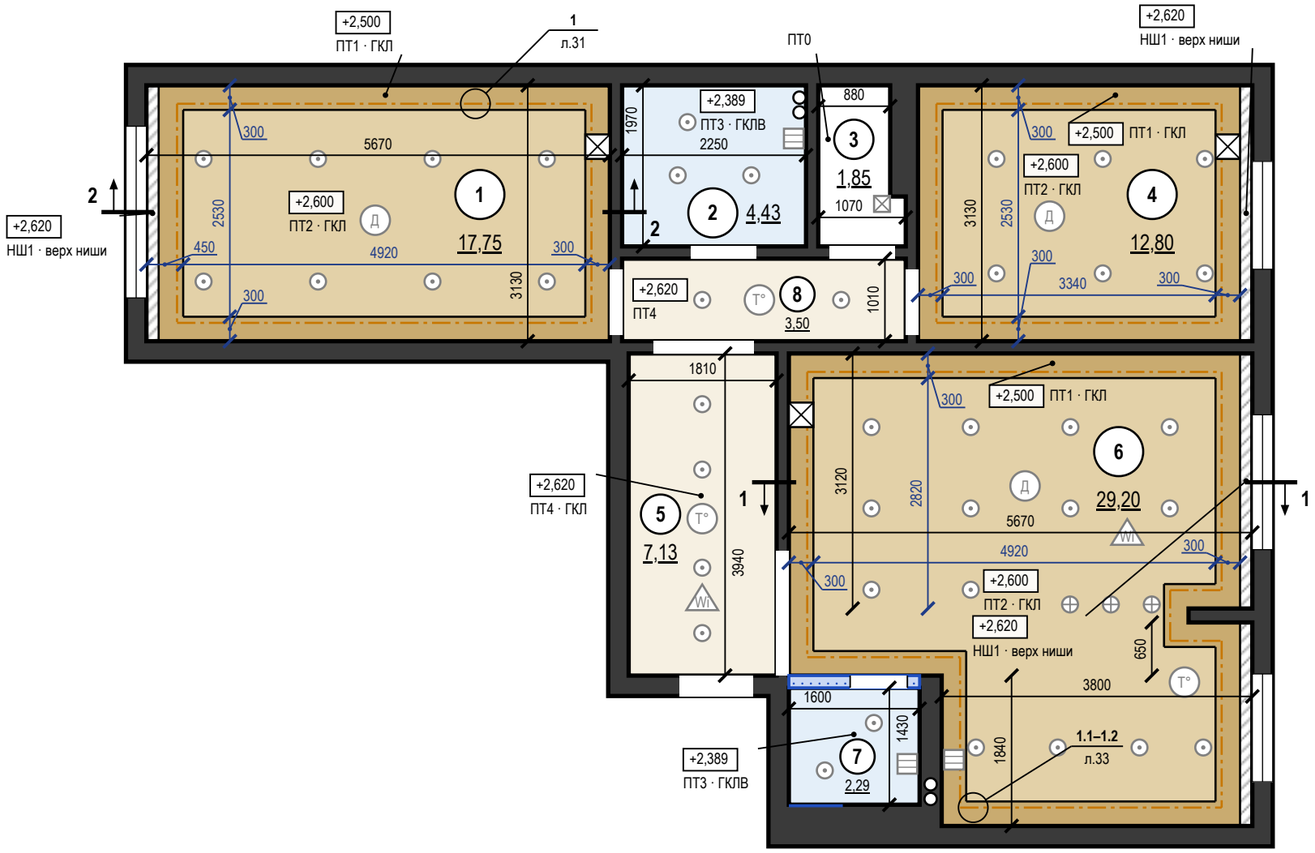

Ведомость потолков

Пом.	Марка	Конструкция	Низ / верх ниши	S, м²	Q
1	ПТ1	ГКЛ П113, короб LED	+2,500	4,83	Q3
1	ПТ2	ГКЛ П113	+2,600	12,45	Q3
1	НШ1	ниша под шторы 150×120	+2,620	0,47	
2	ПТ3	ГКЛВ П113	+2,389	4,43	Q3
3	ПТ0	Существующий потолок, окраска	+2,700	1,85	
4	ПТ1	ГКЛ П113, короб LED	+2,500	3,88	Q3
4	ПТ2	ГКЛ П113	+2,600	8,45	Q3
4	НШ1	ниша под шторы 150×120	+2,620	0,47	
5	ПТ4	ГКЛ П113	+2,620	7,13	Q3
6	ПТ1	ГКЛ П113, короб LED	+2,500	6,80	Q3
6	ПТ2	ГКЛ П113	+2,600	21,56	Q3
6	НШ1	ниша под шторы 150×120	+2,620	0,84	
7	ПТ3	ГКЛВ П113	+2,389	2,29	Q3
8	ПТ4	ГКЛ П113	+2,620	3,50	Q3
		Итого		**78,95**	


Примечания

1. За отметку ±0,000 принят уровень чистого пола сухих помещений (готовое покрытие), а не существующего пола; пол пом. 2, 7 — −0,015; верх плиты перекрытия −0,064 — расчётный по пирогу пола, не замерен; существующий пол снимается до плиты, его отметка не замерена. Отметки в прямоугольниках — низ потолка; низ перекрытия +2,700. Марка потолка — одна конструкция и отметка на весь альбом.
2. Размеры помещений в свету (ширина × длина, мм), не поместившиеся на плане: пом. 3 — 880 × 1360, 1070 × 610; пом. 4 — 4090 × 3130; пом. 6 — 5670 × 3120, 4890 × 170, 5670 × 650, 3800 × 1840; пом. 8 — 3470 × 1010.
3. Потолки ГКЛ — каркасная система П113: подвесы через 1000 (с запасом: СП 163, табл. 14 — до 1100 при 0,15 кН/м²), несущие профили через 500, основные через 1200 мм; листы — поперёк несущих профилей. В помещениях 2, 7 — ГКЛВ на оцинкованном каркасе.
4. Нижний уровень — пояс-короб по периметру шириной 300 мм (карниз подсветки + 150 мм полки), верхний — поле внутри пояса: пом. 1, 4, 6.
5. LED-лента в алюминиевом профиле посередине карниза короба шириной 300 мм (узел 1, лист 31); длина по плану: пом. 1 — 15,5 м (в плане освещения 15,5); пом. 4 — 12,3 м (в плане освещения 12,3); пом. 6 — 22,1 м (в плане освещения 22,1).
6. Ниши под шторы 150×120 мм — на всю длину стены с окном; карниз — на закладной до обшивки (узел 2, лист 31).
7. Примыкание к стенам: теневой шов 15 мм, техзазор 3 мм — пом. 1, 4, 6, по стенам, выровненным штукатуркой (узел 1); пом. 2, 5, 7, 8 — разделительная лента.
8. Светильники и потолочные устройства — подложка с планов освещения, слаботочных систем и вентиляции (положение — по ним); вырезы и закладные — по ведомости на листе, до обшивки; отверстия не совмещать с профилями, глубина корпуса светильника до 70 мм.
9. Разрезы 1–1, 2–2 — на листе 31; высоты мебели и дверных блоков сверены с низом потолка в разрезах.
10. Шпаклевание ГКЛ и условия приёмки — Q3: рассеянный дневной свет, осмотр с 2 м; боковой свет не оценивается.
11. Ведомость вырезов и закладных в потолке — на листе 31; вырезы и закладные — до обшивки.
12. Люки ревизии 300×300 мм — по центру блоков питания LED (БП1, БП2, БП4; координаты — план освещения).
13. ПТ0 — пом. 3: существующий потолок, окраска, без подвесного потолка, низ +2,700; материал и цвет — по ведомости отделки.
14. Сечения потолков М 1:10: пом. 1 — 1.1, 1.2 (лист 33); пом. 4 — 1.1, 1.2 (лист 33).

					Проект: Трёхкомнатная квартира — **М 1:75**
	Лист	№ док.	Подпись	Дата	
Дизайнер	Кырлан А.С.			04.11.26	План потолков
					Стадия: П; Лист: 30; Листов: 92


Разрез 1–1 (М 1:40)

Пом. 6 Кухня-гостиная; линия разреза — план потолков, лист 30

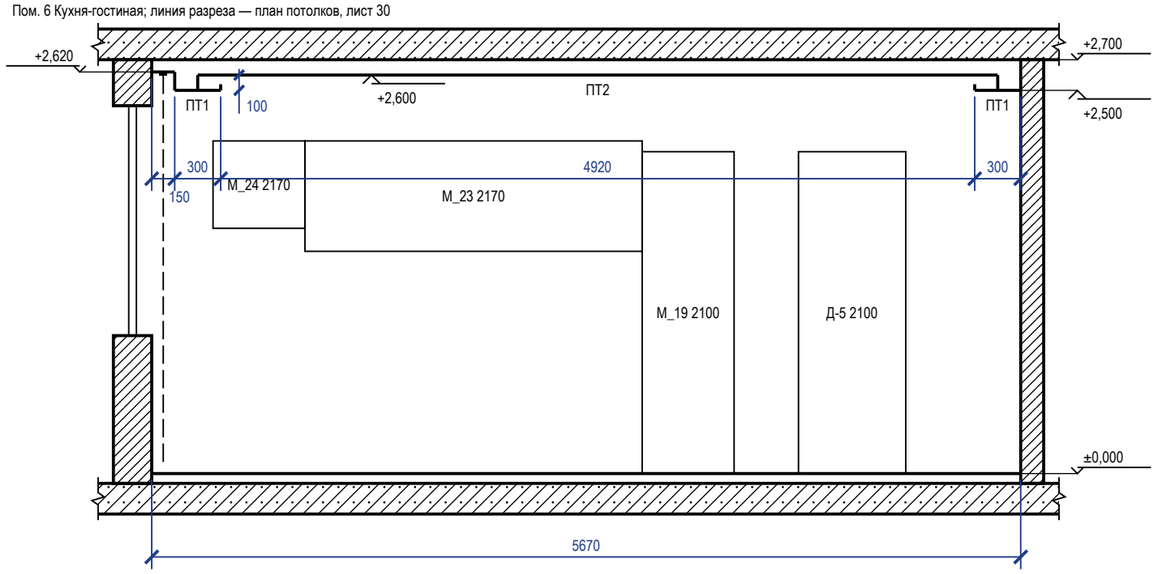


Разрез 2–2 (М 1:40)

Пом. 1 Спальня 1; линия разреза — план потолков, лист 30

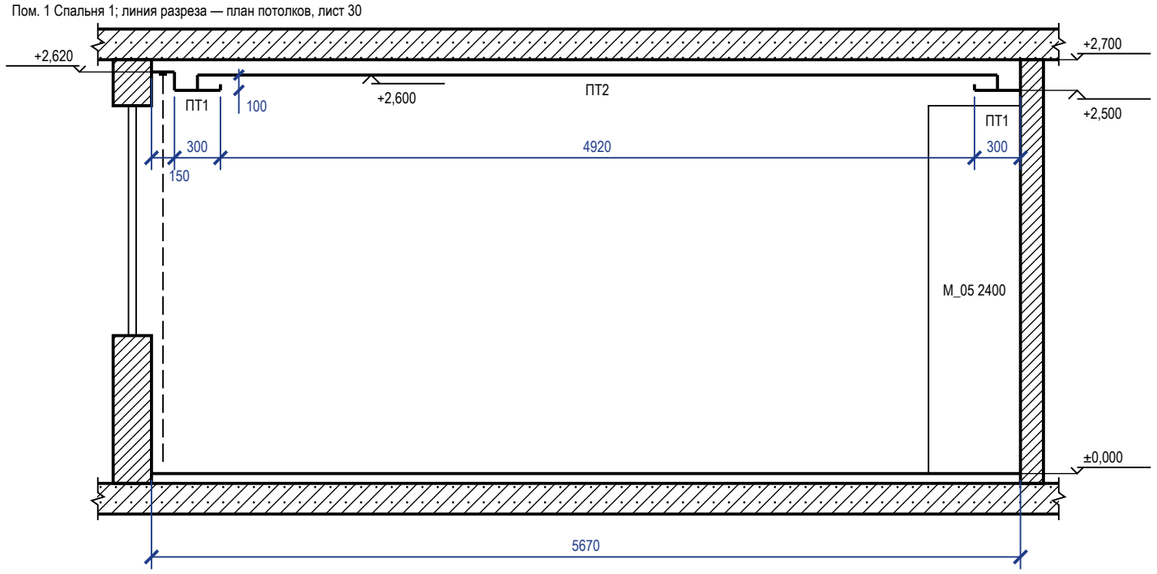

1 Короб с LED-подсветкой, теневой шов (М 1:10)


Пом. 1, 4, 6; карниз 150×100, щель под свет 60 мм

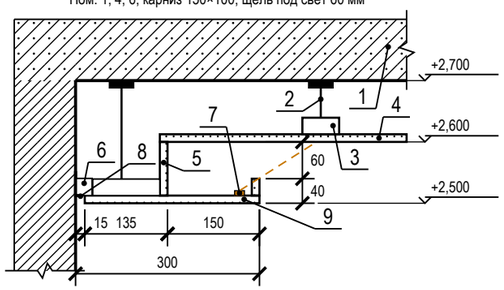

1 — плита перекрытия
2 — подвес прямой, шаг 1000 мм
3 — ПП 60×27: несущие через 500, основные через 1200 мм
4 — ГКЛ 12,5 по П113 — верхний уровень
5 — задняя стенка и бортик карниза — ГКЛ 12,5
6 — ПН 28×27 по периметру, к стене через 500 мм
7 — LED-лента в алюминиевом профиле
8 — теневой профиль: шов 15 мм, зазор 3 мм
9 — низ короба — ГКЛ 12,5 по ПП 60×27

2 Ниша под шторы (М 1:10)

Пом. 1, 4, 6; без подсветки; закладные под карниз — до обшивки

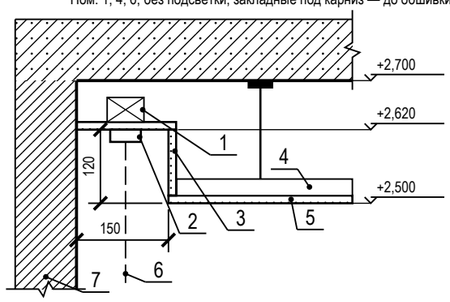

1 — закладная под карниз — брус 40×50
2 — карниз (шина), высота с верхом портьеры 100 мм
3 — стенка и потолок ниши — ГКЛ 12,5
4 — ПП 60×27 — каркас короба
5 — низ короба нижнего уровня — ГКЛ 12,5
6 — портьера
7 — стена с окном

Ведомость вырезов и закладных в потолке

Марка	Устройство	Кол.	Пом.
	Светильник встраиваемый (марки — план освещения)	39	1, 2, 4, 5, 6, 7, 8
	Светильник накладной (марки — план освещения)	1	3
	Светильник подвесной (марки — план освещения)	3	6
ИП1, ИП2, ИП4	Извещатель дымовой	3	1, 4, 6
ИП3, ИП5, ИП6	Извещатель тепловой	3	5, 6, 8
АР1, АР2	Точка доступа Wi-Fi, PoE	2	5, 6
ВР1…ВР3	Решётка вытяжная (вентилятор)	3	2, 6, 7
	Люк ревизии 300×300	3	1, 4, 6

Условные обозначения

- плита перекрытия в сечении
- стена в сечении
- потолок ГКЛ в сечении; под линией — марка потолка (план потолков)
- мебель и дверные проёмы за секущей плоскостью; число — марка и верх от чистого пола, мм
- портьера в нише под шторы

Примечания

1. Разрезы — по линиям 1–1, 2–2 на плане потолков (лист 30). Отметки — от ±0,000 чистого пола, м; размеры — мм.
2. Высоты мебели и дверных блоков за секущей плоскостью сверены с низом потолка над ними: верх ниже низа короба и поля.
3. ГКЛ 12,5 мм по каркасу П113; перепад уровней и бортик карниза — ГКЛ по ПП 60×27 (узел 1 — на этом листе). Ниша под шторы — на всю длину стены с окном, карниз на закладной до обшивки (узел 2 — на этом листе).
4. Толщины плит перекрытия и пирога пола показаны условно.
5. Сечения потолков по помещениям М 1:10 (отметки помещения, профили, подвесы, крепёж, изделия) — лист 33.
6. Ведомость вырезов и закладных в потолке — к плану потолков (лист 30): вырезы и закладные — до обшивки, марки светильников — по плану освещения.
7. Ведомость объёмов потолков (лист ГКЛ, профиль, подвесы, лента, блоки питания, люки) — на листе 32.

					Проект: Трёхкомнатная квартира — М 1:40; 1:10
	Лист	№ док.	Подпись	Дата	
Дизайнер	Кырлан А.С.			04.11.26	Разрезы и узлы потолков
					Стадия: П; Лист: 31; Листов: 92

Ведомость объёмов потолков

Позиция	Ед.	Кол.	Пом.
Лист ГКЛ 12,5	м²	86,10	1, 4, 5, 6, 8
Лист ГКЛВ 12,5	м²	6,72	2, 7
Борта и карнизы (входят в площади листов выше)	м²	15,71	1, 4, 6
Профиль ПП 60×27	м	234,46	1, 2, 4, 5, 6, 7, 8
Профиль ПН 28×27	м	261,30	1, 2, 4, 5, 6, 7, 8
Подвес прямой	шт.	114	1, 2, 4, 5, 6, 7, 8
Анкер-клин к плите	шт.	114	1, 2, 4, 5, 6, 7, 8
Шуруп TN 3,5×25	шт.	2135	1, 2, 4, 5, 6, 7, 8
Лента армирующая для швов	м	111,38	1, 2, 4, 5, 6, 7, 8
Шпаклёвка для швов	кг	37,13	1, 2, 4, 5, 6, 7, 8
Грунтовка (швы)	л	9,28	1, 2, 4, 5, 6, 7, 8
Лента разделительная по периметру	м	91,46	1, 2, 4, 5, 6, 7, 8
Сплошная шпаклёвка и окраска (площадь развёртки)	м²	92,82	1, 2, 4, 5, 6, 7, 8
Лента LED	м	49,90	1, 4, 6
Требуемая мощность блоков питания	Вт	623	1, 4, 6
Установленная мощность блоков питания	Вт	700	1, 4, 6
Блок питания LED	шт.	3	1, 4, 6
Люк ревизии	шт.	3	1, 4, 6

Примечания


1. ГКЛ 12,5 мм по каркасу П113; узлы коробов и ниш под шторы: узел 1 — лист 31; узел 2 — лист 31; условные обозначения разрезов — на листе 31.
2. Ведомость объёмов — по геометрии плана потолков: Лист ГКЛ 12,5 — плоскости уровней + борта (без арочных участков); Лист ГКЛВ 12,5 — плоскости уровней + борта; Борта и карнизы — длина перепада × перепад; Профиль ПП 60×27 — S × (1/шаг несущ. + 1/шаг осн.) + стойки бортов; Профиль ПН 28×27 — периметр стен + 2 × перепады + карнизы; Подвес прямой — по раскладке: S уровня / (шаг осн. × шаг подвесов), пояс уже шага — ряд вдоль пояса, фигура — по контуру; шаг подвесов — не больше табл. 14 СП 163; Анкер-клин к плите — по одному на подвес (Knauf П113); Шуруп TN 3,5×25 — 23 шт./м² (Knauf П113, табл. 2 альбома П 11); Лента армирующая для швов — 1,2 м/м² листа (Knauf); Шпаклёвка для швов — 0,4 кг/м² листа, только швы (Knauf); Грунтовка (швы) — 0,1 л/м² листа, только швы (Knauf); Лента разделительная по периметру — периметр стен под потолком ГКЛ; Сплошная шпаклёвка и окраска (площадь развёртки) — плоскости + борта; расход — по паспорту материала (норма расхода на сплошной слой не подтверждена); Лента LED — по оси карниза и ниши фигуры (план потолков); Требуемая мощность блоков питания — Вт/м × длина × 1,3; Установленная мощность блоков питания — сумма мощностей блоков по плану освещения; Блок питания LED — блоки потолочных лент по плану освещения (БП1, БП2, БП4); Люк ревизии — план потолков; без запаса на подрезку (при закупке листа: ×1,075 при S > 20 м², ×1,175 — 10–20 м², ×1,275 — < 10 м²).

					Проект: Трёхкомнатная квартира
	Лист	№ док.	Подпись	Дата	
Дизайнер	Кырлан А.С.			04.11.26	Разрезы и узлы потолков (продолжение)

Стадия	Лист	Листов
П	32	92

Сечение 1.1. Короб с LED-подсветкой, теневой шов (М 1:10)

Пом. 1 Спальня 1, 4 Спальня 2, 6 Кухня-гостиная; карниз 150×100, щель под свет 60 мм

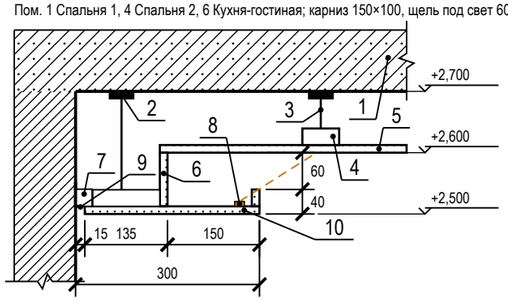

1 — плита перекрытия

2 — анкер-клин к плите — по одному на подвес

3 — подвес прямой, шаг 1000 мм

4 — ПП 60×27: несущие через 500, основные через 1200 мм; соединители одноуровневые, шурупы LN 3,5×9

5 — ГКЛ 12,5 по П113 — верхний уровень; шурупы TN 3,5×25 через 170 мм

6 — задняя стенка и бортик карниза — ГКЛ 12,5

7 — ПН 28×27 по периметру — дюбель-гвоздь через ≤ 500 мм, не менее 3 на профиль


8 — LED-лента 9,6 Вт/м, 24 В в алюминиевом профиле

9 — теневой профиль: шов 15 мм, зазор 3 мм

10 — низ короба — ГКЛ 12,5 по ПП 60×27

Сечение 1.2. Ниша под шторы (М 1:10)

Пом. 1 Спальня 1, 4 Спальня 2, 6 Кухня-гостиная; без подсветки; закладные под карниз — до обшивки

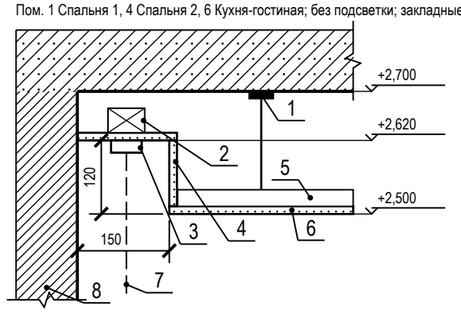

1 — анкер-клин к плите — по одному на подвес; подвес прямой, шаг 1000 мм

2 — закладная под карниз — брус 40×50

3 — карниз (шина), высота с верхом портьеры 100 мм

4 — стенка и потолок ниши — ГКЛ 12,5

5 — ПП 60×27 — каркас короба, основные через 1200 мм; соединители одноуровневые, шурупы LN 3,5×9

6 — низ короба нижнего уровня — ГКЛ 12,5; шурупы TN 3,5×25 через 170 мм

7 — портьера

8 — стена с окном


Условные обозначения

— · — LED-лента в нише подсветки (карниз короба, ниша фигуры)

Примечания

1. Сечения потолков М 1:10 по помещениям с нишами LED и нишами под шторы: отметки и размеры этого помещения от ±0,000 чистого пола (м, мм). Положение — по плану потолков (лист 30): короб и ниша LED — по линиям ленты, ниша под шторы — у стены с окном; типовые узлы по группам помещений — на листе 31.
2. Крепёж: подвес прямой к плите на анкер-клине — по одному на подвес (Knauf П113); ПН к стенам — дюбель-гвоздь через ≤ 500 мм, не менее 3 на профиль (серия 1.045.9-2.08); лист 12,5 — шурупы TN 3,5×25 через 170 мм (СП 163, табл. 15); профили между собой — соединители одноуровневые, шурупы LN 3,5×9.
3. Изделие карниза, профиля LED и галтели подписано артикулом из данных; где артикул не выбран, сечение дано по габаритам из данных (ширина и глубина ниши, щель под свет), изделие подбирается по ним.

					Проект: Трёхкомнатная квартира	М 1:10
	Лист	№ док.	Подпись	Дата		
Дизайнер	Кырлан А.С.			04.11.26	Сечения потолков М 1:10	Стадия / Лист / Листов
						П / 33 / 92

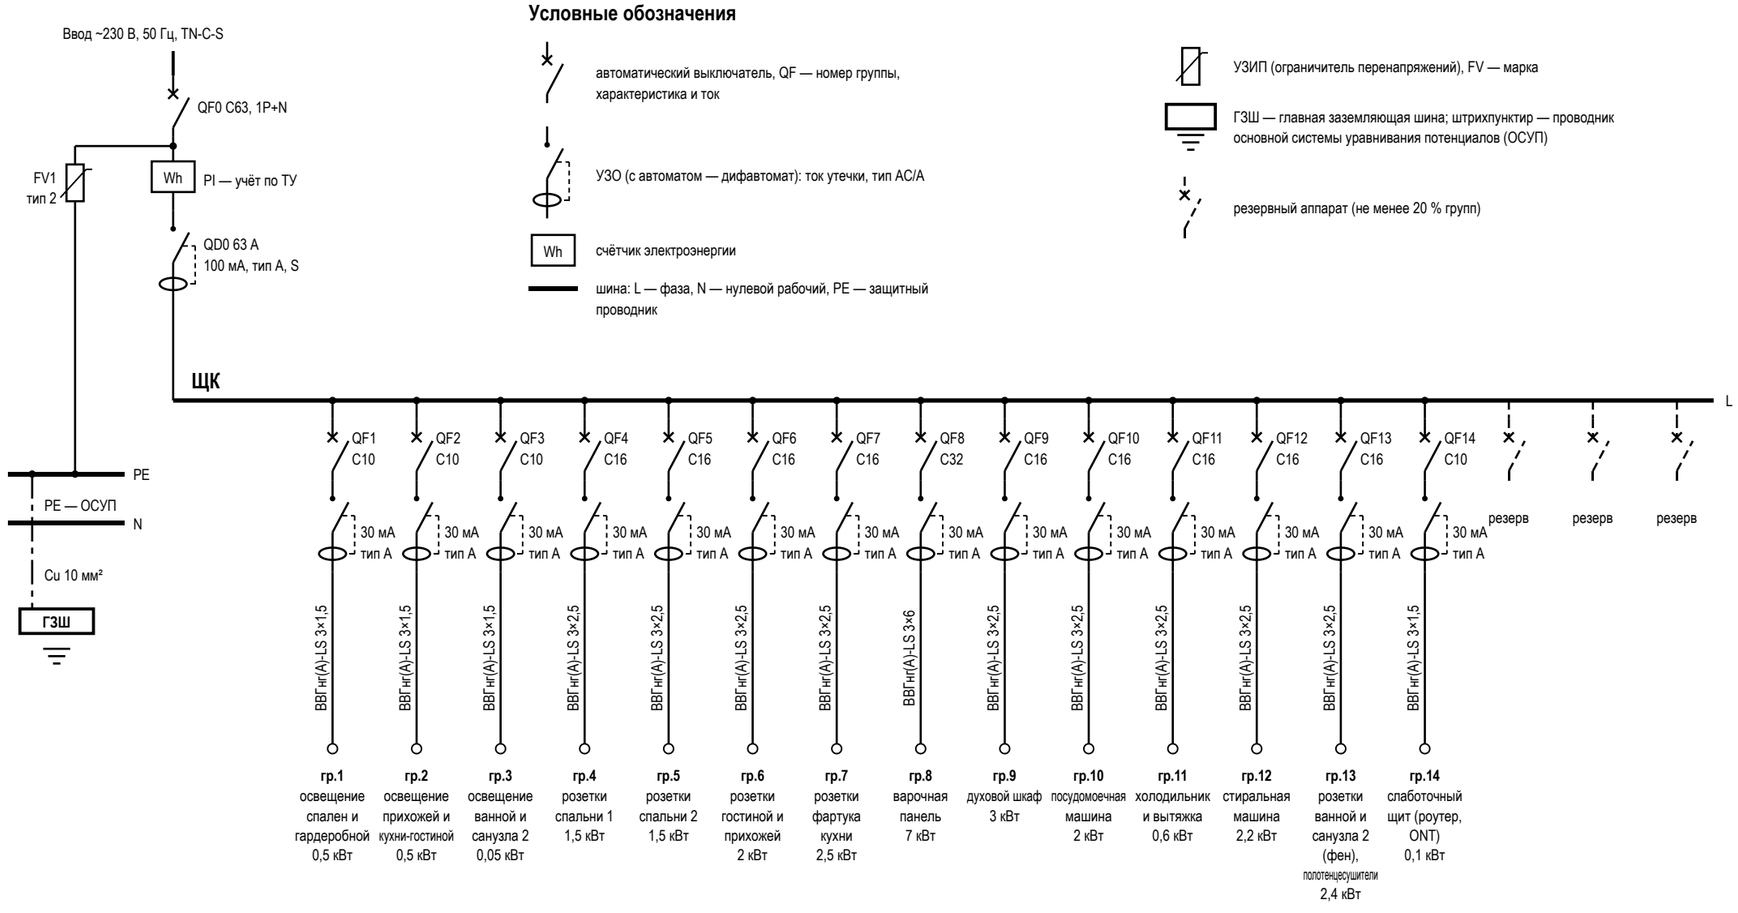

Условные обозначения

- автоматический выключатель, QF — номер группы, характеристика и ток
- УЗО (с автоматом — дифавтомат): ток утечки, тип AC/A
- Wh — счётчик электроэнергии
- шина: L — фаза, N — нулевой рабочий, PE — защитный проводник
- УЗИП (ограничитель перенапряжений), FV — марка
- ГЗШ — главная заземляющая шина; штрихпунктир — проводник основной системы уравнивания потенциалов (ОСУП)
- резервный аппарат (не менее 20 % групп)

Данные щитка

Показатель	Значение
Номер щитка	ЩК
Тип	ЩРВ-П-48, IP41
Уст. мощность, кВт	25,85
Разреш. мощность, кВт	15
Расчётная, кВт	11,8
Автоматы 1п: занят. / рез.	14 / 3
Модулей: всего / занято	48 / 34
Ток на вводе, А	63
Вводной аппарат	QF0 C63, 1P+N
УЗИП	FV1, тип 2, ЩК, после счётчика
ГЗШ, проводник ОСУП	Cu 10 мм²

Таблица групп щита ЩК и кабельный журнал


№	Назначение	Помещения	Автомат	УЗО / дифавтомат	Кабель	Длина, м	P, кВт	Точек
1	освещение спален и гардеробной	1, 3, 4, 8	C10	30 мА, тип A	ВВГнг(A)-LS 3×1,5	94,2	0,5	30
2	освещение прихожей и кухни-гостиной	5, 6, 8	C10	30 мА, тип A	ВВГнг(A)-LS 3×1,5	91,2	0,5	38
3	освещение ванной и санузла 2	2, 6, 7, 8	C10	30 мА, тип A	ВВГнг(A)-LS 3×1,5	58,2	0,05	11
4	розетки спальни 1	1	C16	30 мА, тип A	ВВГнг(A)-LS 3×2,5	31,1	1,5	6
5	розетки спальни 2	4	C16	30 мА, тип A	ВВГнг(A)-LS 3×2,5	30,3	1,5	6
6	розетки гостиной и прихожей	5, 6, 8	C16	30 мА, тип A	ВВГнг(A)-LS 3×2,5	52,1	2	10
7	розетки фартука кухни	6	C16	30 мА, тип A	ВВГнг(A)-LS 3×2,5	28,2	2,5	6
8	варочная панель	6	C32	30 мА, тип A	ВВГнг(A)-LS 3×6	15,4	7	1
9	духовой шкаф	6	C16	30 мА, тип A	ВВГнг(A)-LS 3×2,5	15,5	3	1
10	посудомоечная машина	6	C16	30 мА, тип A	ВВГнг(A)-LS 3×2,5	14,4	2	1
11	холодильник и вытяжка	6	C16	30 мА, тип A	ВВГнг(A)-LS 3×2,5	14,2	0,6	2
12	стиральная машина	2	C16	30 мА, тип A	ВВГнг(A)-LS 3×2,5	13,2	2,2	1
13	розетки ванной и санузла 2 (фен), полотенцесушители	2, 7	C16	30 мА, тип A	ВВГнг(A)-LS 3×2,5	31,9	2,4	4
14	слаботочный щит (роутер, ONT)	5	C10	30 мА, тип A	ВВГнг(A)-LS 3×1,5	3,6	0,1	1
	Итого по сечениям ВВГнг(A)-LS, м: 3×1,5 — 247,2; 3×2,5 — 230,9; 3×6 — 15,4					493,5		

Примечания

1. Схема однолинейная: одна линия — фаза, N и PE группы; аппараты — в отключённом положении (ГОСТ 2.702, ГОСТ 2.755). Номера групп — как у точек на планах (гр.). За отметку 0,000 принят уровень чистого пола; высота щита — по плану розеток.
2. Розеточные и мокрые линии — через УЗО или дифавтомат с током утечки не более 30 мА (ПУЭ 7.1.79); в санузле выполнить ДСУП (ПУЭ 7.1.87–7.1.88).
3. УЗО тип A — для линий с электроникой, стиральной и посудомоечной машиной, LED-драйверами; тип AC — только для чисто активной нагрузки.
4. Кабель — медный, исполнение нг(A)-LS (ГОСТ 31565-2012); скрытая прокладка только горизонтально и вертикально, фактические трассы зафиксировать исполнительной схемой до закрытия отделкой.
5. Номинал автомата — не выше допустимого тока кабеля: 1,5 мм² — до 10 А, 2,5 мм² — до 16 А. Резерв щита — не менее 20 % модулей.
6. Расчёт нагрузок, токов КЗ, селективности и сечений — по проекту ЭОМ организации с допуском СРО; лист задаёт состав, расположение и группы.
7. УЗИП FV1 — после вводного автомата, проводник к шине PE — кратчайший, без петель. Шина PE щита соединяется с ГЗШ проводником ОСУП; к ГЗШ присоединяются трубы водопровода и отопления на вводе в квартиру (ПУЭ 7.1.87). Шины N и PE — раздельные, после разделения PEN не объединяются.
8. До подключения нагрузки — приёмо-сдаточные испытания с протоколом: сопротивление изоляции линий не менее 0,5 МОм, срабатывание УЗО по току и времени, непрерывность защитных проводников PE (ПУЭ, гл. 1.8).

					Проект: Трёхкомнатная квартира
	Лист	№ док.	Подпись	Дата	
Дизайнер	Кырлан А.С.			04.11.26	Однолинейная схема щита

Стадия	Лист	Листов
П	34	92

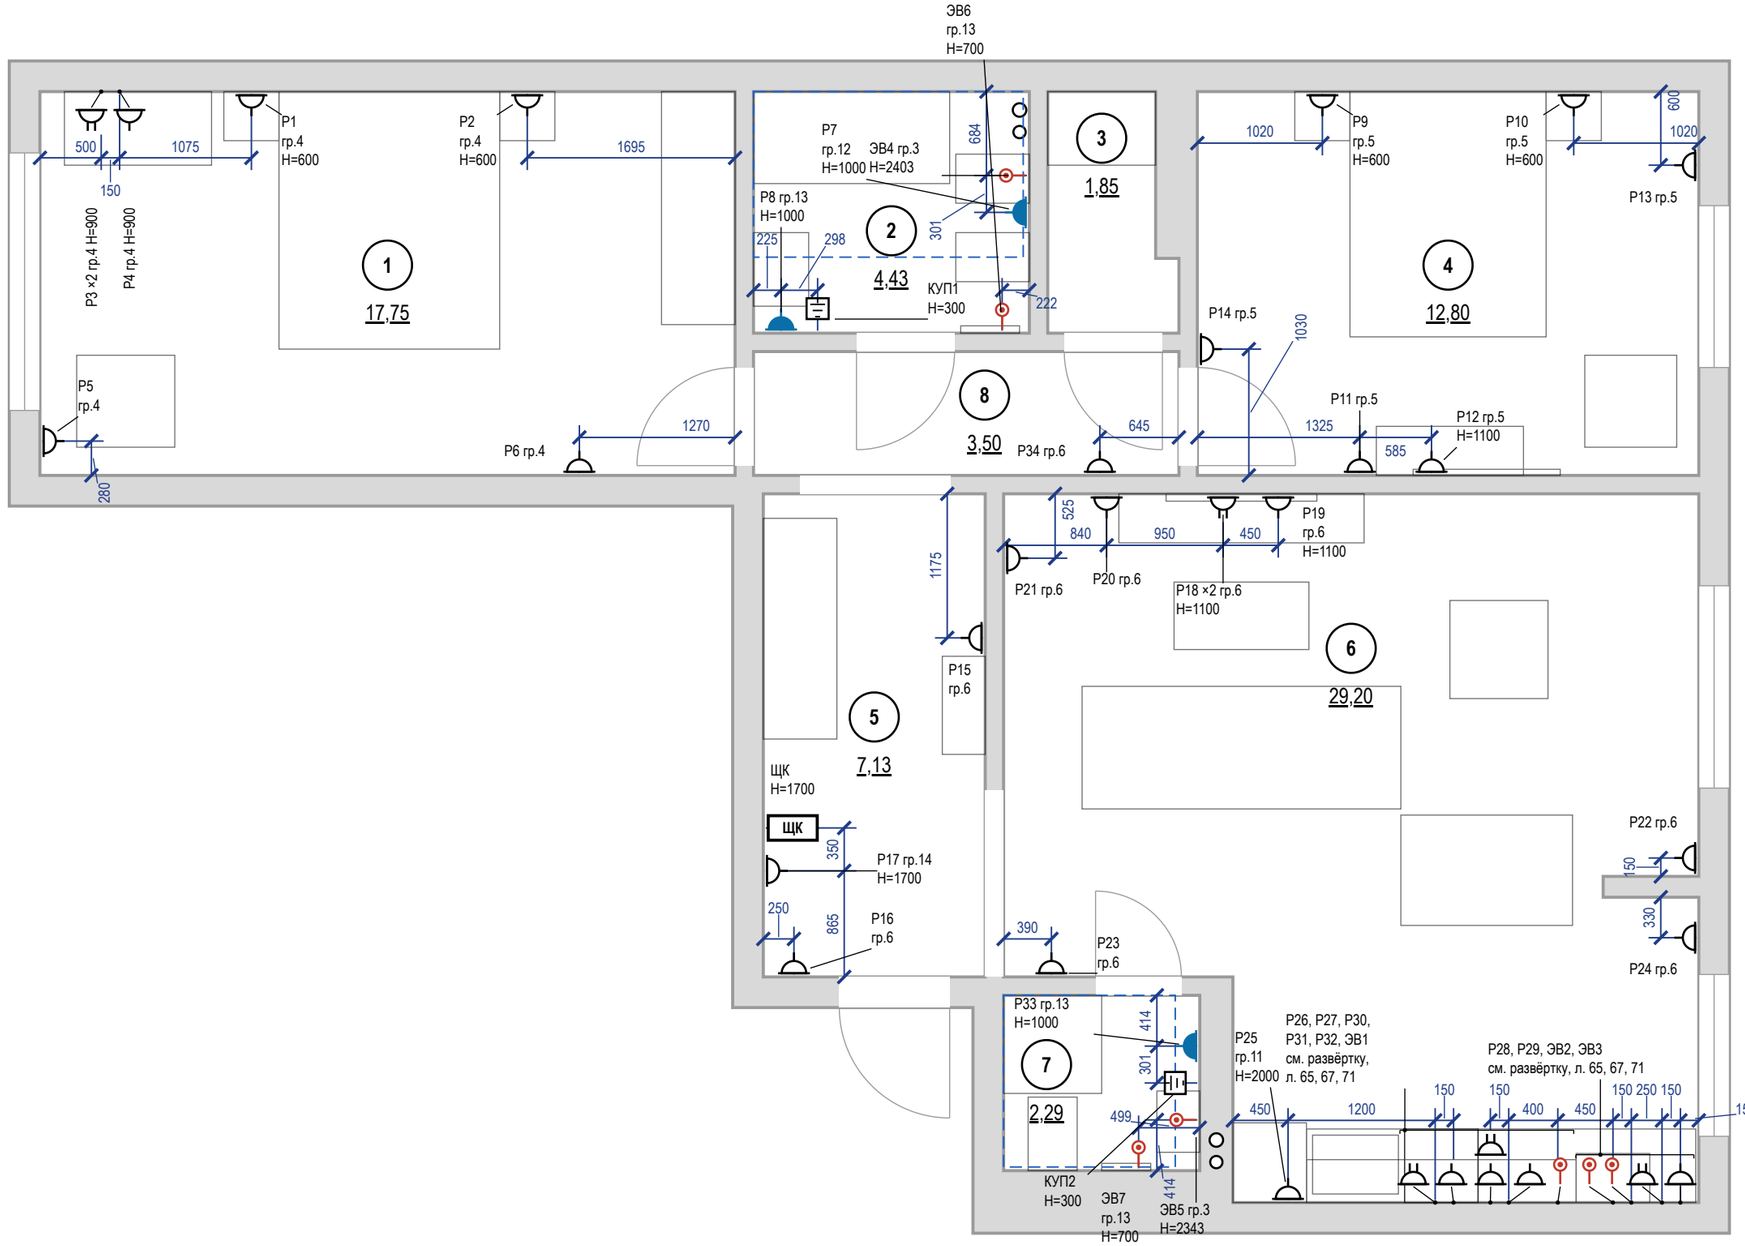

Условные обозначения

Знак	Тип изделия	H, мм	Кол., шт
	Розетка с заземлением	300	14
	То же	у знака	12
	Блок розеток с заземлением, рамка 2 поста	у знака	5
	Розетка с заземлением IP44	1000	3
	Вывод кабеля к прибору	у знака	7
	КУП (уравнивание потенциалов)	300	2
ЩК	Щит квартирный	1700	1

розетка с заземляющим контактом; у знака — марка, ×N — постов в рамке, гр. — группа щита, H — высота оси, мм

знак разведён для читаемости: точка на стене — у выноски, привязка — до неё

граница зоны 2 ванной (600 мм от ванны/поддона)

мебель и сантехприборы — подложка

стояк: К1 — канализация, В1 — ХВС, Т3 — ГВС


1 — номер помещения, площадь м²

Итого розеток (механизмов) — 39 шт; рамок — 34 шт: на 1 пост — 29, на 2 поста — 5.

Примечания

1. За отметку 0,000 принят уровень чистого пола. Высоты H — от чистого пола до оси изделия; привязки — от чистовой грани стены до оси механизма (у рамки на несколько постов — до оси рамки).
2. Розетки без отметки H у знака — на высоте 300 мм от чистого пола до оси механизма; выводы кабеля — по паспорту прибора.
3. Розетки в санузле — только вне зон 0–2 (ПУЭ 7.1.48, ГОСТ Р 50571.7.701-2024), IP44, через УЗО 30 мА.
4. Розеточные и мокрые линии — через УЗО или дифавтомат с током утечки не более 30 мА (ПУЭ 7.1.79); в санузле выполнить ДСУП (ПУЭ 7.1.87–7.1.88).
5. Кабель — медный, исполнение нг(А)-LS (ГОСТ 31565-2012); скрытая прокладка только горизонтально и вертикально, фактические трассы зафиксировать исполнительной схемой до закрытия отделкой.
6. Расчёт нагрузок, токов КЗ, селективности и сечений — по проекту ЭОМ организации с допуском СРО; лист задаёт состав, расположение и группы.
7. Выводы кухонной техники — после утверждения проекта кухни (ориентировочно); привязки выводов даны от осей модулей гарнитура и пересматриваются вместе с проектом кухни.
8. Электрический тёплый пол проектом не предусмотрен; при решении заказчика устроить — отдельный лист «План тёплых полов»: контуры с отступом 100 мм от стен и мебели без ножек, датчик в гофре, терморегулятор, своя группа щита через УЗО 30 мА.

					Проект: Трёхкомнатная квартира	**М 1:50**
	Лист	№ док.	Подпись	Дата		
Дизайнер	Кырлан А.С.			04.11.26	План розеток и электровыводов	Стадия: П; Лист: 35; Листов: 92

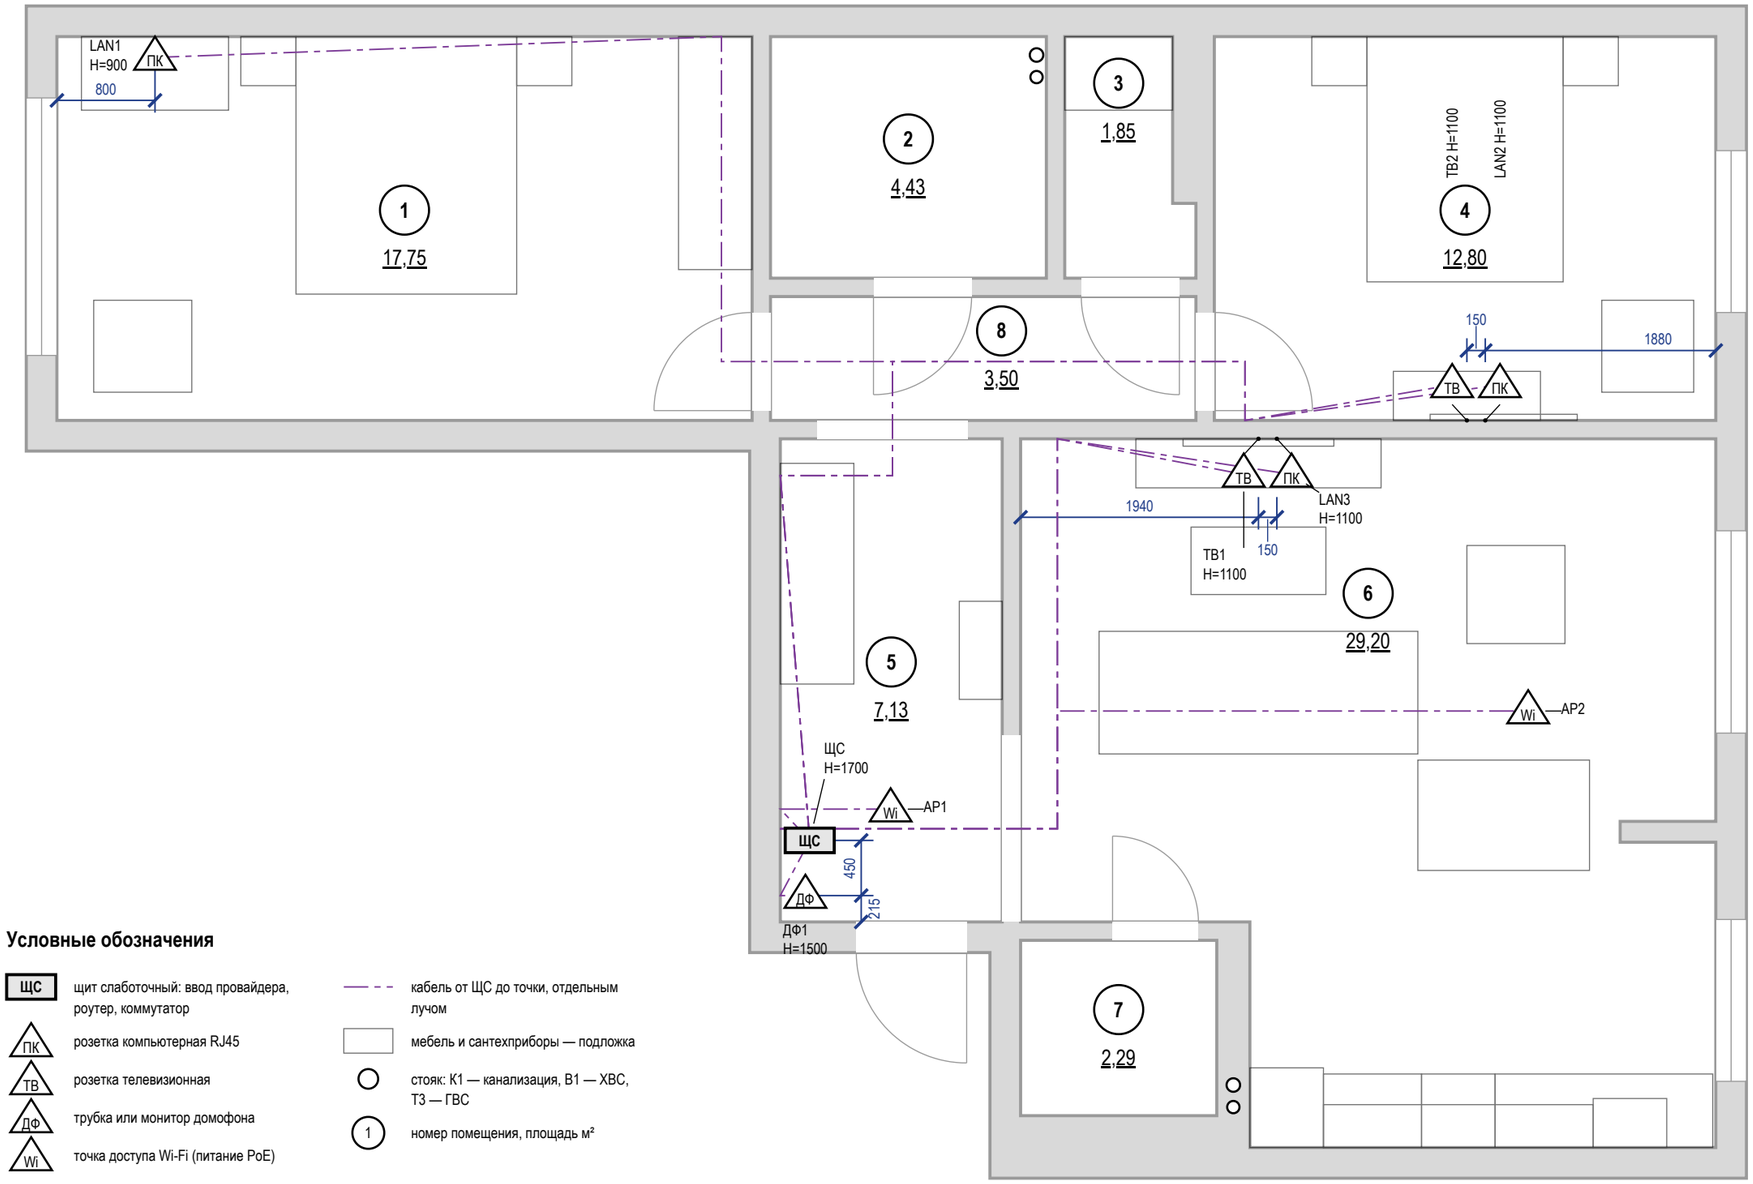


Условные обозначения

ЩС	щит слаботочный: ввод провайдера, роутер, коммутатор
ПК	розетка компьютерная RJ45
ТВ	розетка телевизионная
ДФ	трубка или монитор домофона
Wi	точка доступа Wi-Fi (питание PoE)
— — —	кабель от ЩС до точки, отдельным лучом
▭	мебель и сантехприборы — подложка
○	стояк: К1 — канализация, В1 — ХВС, Т3 — ГВС
1	номер помещения, площадь м²

Примечания

1. За отметку 0,000 принят уровень чистого пола. Высоты Н — от чистого пола до оси изделия; привязки — от чистовой грани стены до оси механизма (у рамки на несколько постов — до оси рамки).
2. Высота установки, не указанная на плане: розетки LAN и ТВ — 300 мм от чистого пола.
3. Слаботочные кабели — отдельно от силовых: в своей трубе или лотке, при параллельной прокладке не ближе 100 мм к силовым, пересечения под прямым углом; каждую точку — отдельным кабелем от ЩС без скруток.
4. Трассы на листе — принципиальные; фактические зафиксировать исполнительной схемой до закрытия отделкой. Силовые линии, УЗО 30 мА, ДСУП, кабель нг(А)-LS — по листам розеток и щита.
5. Проект силовой части и расчёт токов КЗ — по проекту ЭОМ; слаботочная часть согласуется с провайдером и управляющей компанией (домофон, коллективное ТВ).

					Проект: Трёхкомнатная квартира	М 1:50
	Лист	№ док.	Подпись	Дата		
Дизайнер	Кырлан А.С.			04.11.26	План слаботочных сетей	Стадия: П; Лист: 36; Листов: 92

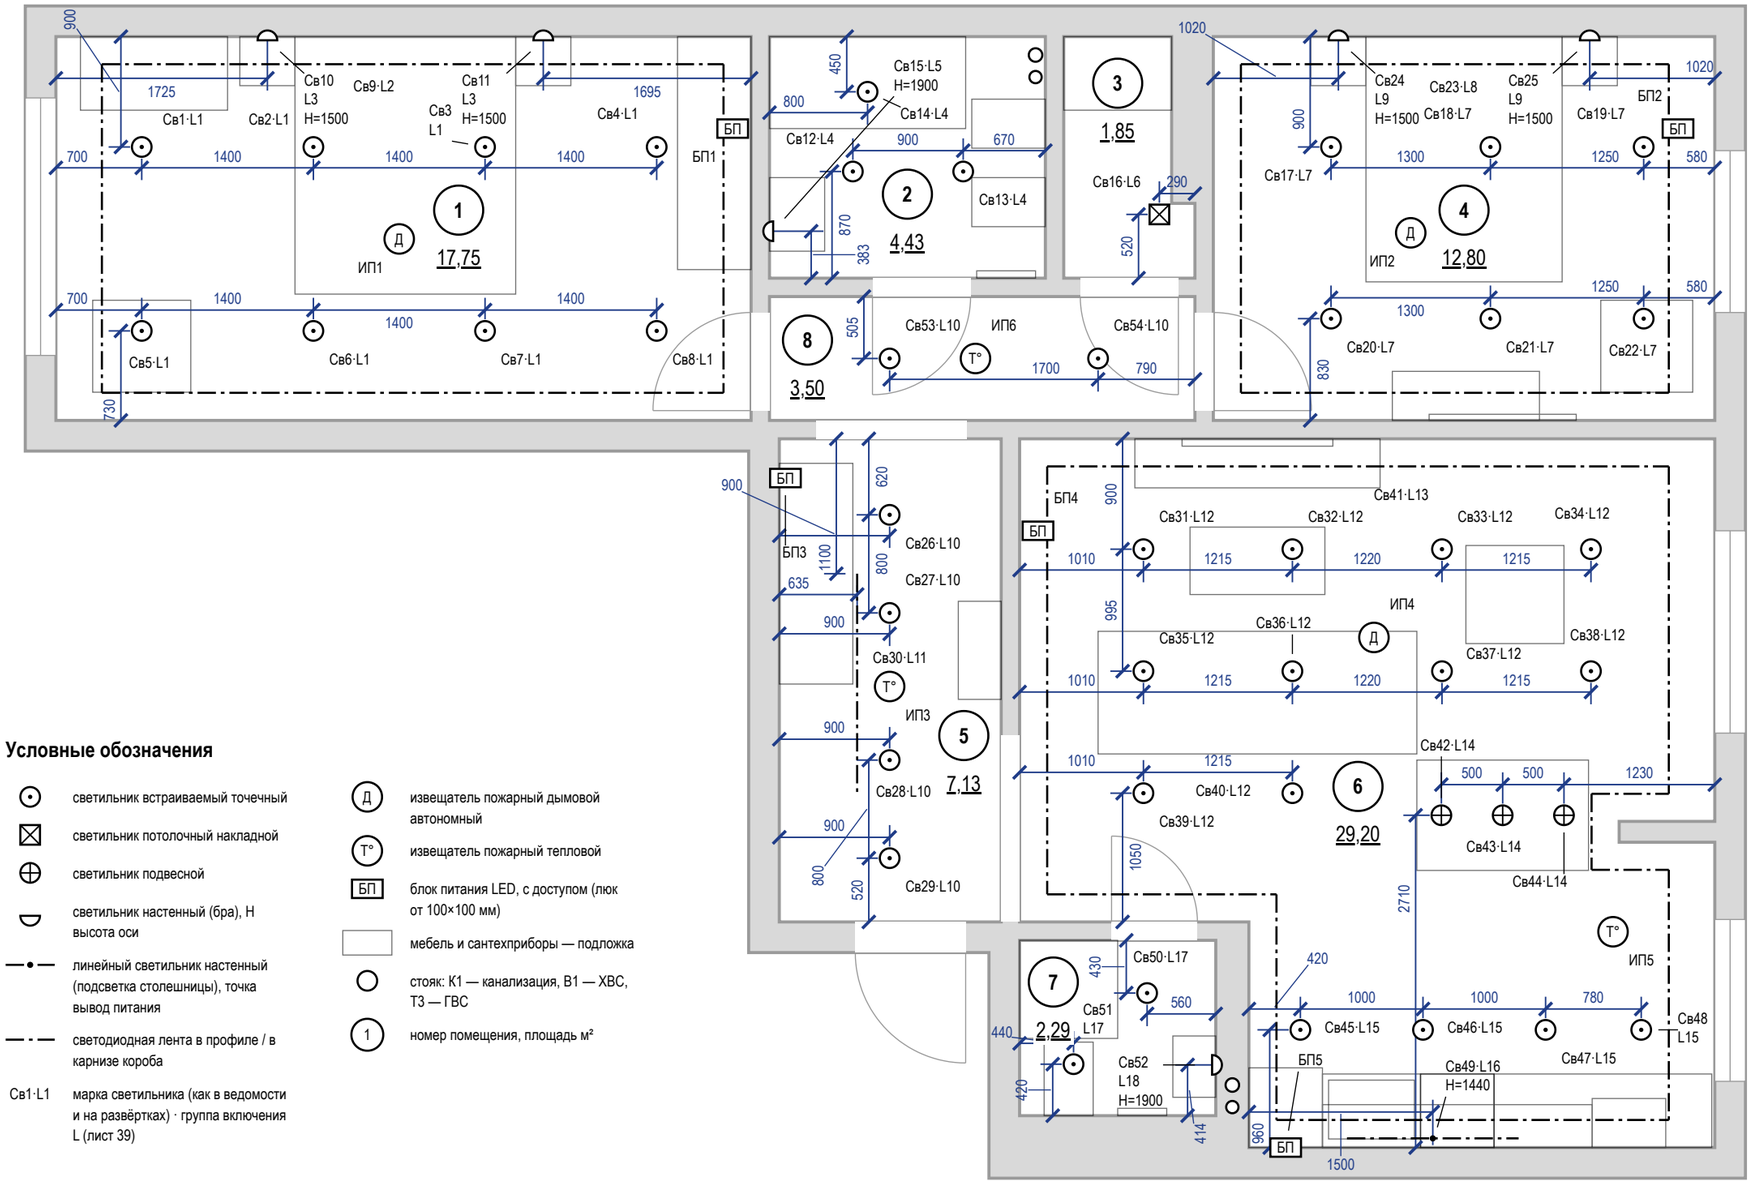

Условные обозначения

⊙	светильник встраиваемый точечный
⊠	светильник потолочный накладной
⊕	светильник подвесной
◡	светильник настенный (бра), H высота оси
—•—	линейный светильник настенный (подсветка столешницы), точка вывод питания
—·—	светодиодная лента в профиле / в карнизе короба
Св1·L1	марка светильника (как в ведомости и на развёртках) · группа включения L (лист 39)
Д	извещатель пожарный дымовой автономный
Т°	извещатель пожарный тепловой
БП	блок питания LED, с доступом (люк от 100×100 мм)
▭	мебель и сантехприборы — подложка
○	стояк: К1 — канализация, В1 — ХВС, Т3 — ГВС
1	номер помещения, площадь м²

Примечания

1. За отметку 0,000 принят уровень чистого пола. Высоты H — от чистого пола до оси изделия; привязки — от чистовой грани стены до оси механизма (у рамки на несколько постов — до оси рамки).
2. Высота установки, не указанная на плане: светильники — на потолке; настенные — по отметке H у знака. Привязки — до оси светильника от чистовой грани стены, по рядам.
3. Во влажных помещениях — светильники не ниже IP44; в зонах 0–2 ванной — по ГОСТ Р 50571.7.701-2024 (зона 1 — IPX5).
4. LED-лента в карнизе подсветки короба — по линии карниза с плана потолков; блок питания — в люке короба (БП на плане), питание ленты длиннее 5 м — с двух концов.
5. Розеточные и мокрые линии — через УЗО или дифавтомат с током утечки не более 30 мА (ПУЭ 7.1.79); в санузле выполнить ДСУП (ПУЭ 7.1.87–7.1.88).
6. Кабель — медный, исполнение нг(A)-LS (ГОСТ 31565-2012); скрытая прокладка только горизонтально и вертикально, фактические трассы зафиксировать исполнительной схемой до закрытия отделкой.
7. Расчёт нагрузок, токов КЗ, селективности и сечений — по проекту ЭОМ организации с допуском СРО; лист задаёт состав, расположение и группы.
8. Ведомость светильников (тип, количество, мощность, поток, Tц, Ra) — лист 38.

	Лист	№ док.	Подпись	Дата
Дизайнер	Кырлан А.С.			04.11.26

Проект: Трёхкомнатная квартира — **М 1:50**

План освещения

Стадия	Лист	Листов
П	37	92

Параметры светильников для подбора

Поз.	Марки	Наименование	Установка	Кол.	P, Вт	Σ P, Вт	Ф, лм	Тц, К	Ra	Угол, °	IP	Дим.	Слой	Группа	Пом.
1	Св1–Св8	Встраиваемый точечный	в ГКЛ, корпус ≤ 70 мм	8	12	96	1000	2700	90	—	20	—	общий	L1	1
2	Св9	Лента светодиодная 24 В	в карнизе короба, профиль с рассеивателем	15,5 м	9,6/м	148,8	900/м	2700	90	—	20	да	акцентный	L2	1
3	Св10, Св11, Св24, Св25	Настенный (бра)	на стене, H=1500	4	6	24	400	2700	90	60	20	—	рабочий	L3, L9	1, 4
4	Св12–Св14, Св51	Встраиваемый точечный	в ГКЛ, корпус ≤ 70 мм	4	6	24	500	3000	90	—	44	—	общий	L4, L17	2, 7
5	Св15, Св52	Настенный светильник над зеркалом, драйвер встроен	над зеркалом, H=1900	2	8	16	600	3000	90	—	44	—	рабочий	L5, L18	2, 7
6	Св16	Потолочный накладной	на потолке, засветка стены	1	10	10	900	3000	90	—	20	—	общий	L6	3
7	Св17–Св22	Встраиваемый точечный	в ГКЛ, корпус ≤ 70 мм	6	12	72	1050	2700	90	—	20	—	общий	L7	4
8	Св23	Лента светодиодная 24 В	в карнизе короба, профиль с рассеивателем	12,3 м	9,6/м	118,5	900/м	2700	90	—	20	да	акцентный	L8	4
9	Св26–Св29, Св53, Св54	Встраиваемый точечный	в ГКЛ, корпус ≤ 70 мм	6	7	42	600	3000	90	—	20	—	общий	L10	5, 8
10	Св30	Лента светодиодная 24 В	на поверхности, профиль с рассеивателем, датчик движения	1,8 м	4,8/м	8,6	150/м	2700	90	—	20	нет	ночной	L11	5
11	Св31, Св32, Св33, Св34, Св35, Св36, Св37, Св38, Св39, Св40	Встраиваемый точечный	в ГКЛ, корпус ≤ 70 мм	10	12	120	1000	3000	90	—	20	да	общий	L12	6
12	Св41	Лента светодиодная 24 В	в карнизе короба, профиль с рассеивателем	22,1 м	9,6/м	211,8	900/м	2700	90	—	20	да	акцентный	L13	6
13	Св42, Св43, Св44	Подвесной	подвес, низ H=1450	3	9	27	800	3000	90	—	20	да	общий	L14	6
14	Св45–Св48	Встраиваемый точечный	в ГКЛ, корпус ≤ 70 мм	4	10	40	900	3000	90	—	20	—	общий	L15	6
15	Св49	Линейный настенный	под верхними шкафами, H=1440	1	18	18	1500	3000	90	—	20	да	рабочий	L16	6
16	Св50	Встраиваемый точечный	в ГКЛ, корпус ≤ 70 мм	1	7	7	600	3000	90	—	44	—	общий	L17	7
		Итого		**50 шт + 51,7 м**		**983,7**									

LED-ленты, линейные светильники и блоки питания

Марка	Пом.	L, м	U, В	Вт/м	Σ P, Вт	БП	P БП, Вт	Загр., %	Питание	Доступ к БП
Св9	1	15,5	24	9,6	148,8	БП1	200	74	с двух концов	люк 300×300 в коробе потолка ПТ1
Св23	4	12,3	24	9,6	118,5	БП2	200	59	с двух концов	люк 300×300 в коробе потолка ПТ1
Св30	5	1,8	24	4,8	8,6	БП3	20	43	с одного конца	в шкафу M_13, верхняя полка
Св41	6	22,1	24	9,6	211,8	БП4	300	71	с двух концов	люк 300×300 в коробе потолка ПТ1
Св49	6	3	24	—	18	БП5	60	30	встроенный ввод	в пенале M_19, верх, съёмная панель

Сценарии (помещения со светорегуляторами)


Помещение	Сценарий	Горят группы (уровень)	Управление
6. Кухня-гостиная	Вечер	L12 споты гостиной — 30 %; L13 подсветка короба — 100 %; L14 подвесы над столом — 50 %; остальные выкл.	светорегуляторы S10, S11, S17
	Ужин	L13 подсветка короба — 60 %; L14 подвесы над столом — 100 %; L16 подсветка столешницы — 30 %; остальные выкл.	светорегуляторы S11, S12, S17
	Кино	L13 подсветка короба — 20 %; остальные выкл.	светорегулятор S17
	Готовка	L12 споты гостиной — 50 %; L15 споты кухни — вкл.; L16 подсветка столешницы — 100 %; остальные выкл.	светорегуляторы S10, S12; выключатель S18

Примечания

1. Позиции и марки Св — те же, что на плане освещения (лист 37); группы L — по плану выключателей (лист 39).
2. Модели светильников не выбраны: лист — техническое задание на подбор. Модель по строке таблицы: поток, Тц, Ra, угол, IP и регулировка яркости не хуже указанных, мощность не больше; встраиваемые — под глубину короба (графа «Установка»). IP 20 — сухие помещения. После выбора моделей (артикул, производитель) лист выпускается как «Спецификация светильников».
3. Длина LED-ленты в карнизе — по линии карниза плана потолков (лист 30); Σ P = Вт/м × длина. Блок питания загружен не больше чем на 80 %; лента 24 В длиннее 10 м питается с двух концов; доступ к блоку питания — люк ревизии 300×300 мм или место, указанное в таблице.
4. Сценарии: % — яркость группы на светорегуляторе; «вкл.» — группа на обычной клавише; группы, не названные в строке, выключены. Светильники и блоки питания групп на светорегуляторе — с регулировкой яркости. Клавиши и светорегуляторы — лист 39.
5. В пом. 1, 4 свет включается клавишами групп — лист 39. Общий сценарий «Ушёл» без системы управления светом не выполняется: группы включают и выключают клавишами.
6. Мощность и поток в таблице — требования к подбору (поток не меньше, мощность не больше указанных); после выбора модели — по её паспорту, Σ P — установленная мощность освещения. Оценка освещённости — на плане освещения; это не светотехнический расчёт.

					Проект: Трёхкомнатная квартира
	Лист	№ док.	Подпись	Дата	
Дизайнер	Кырлан А.С.			04.11.26	Техническое задание на подбор светильников

Стадия	Лист	Листов
П	38	92

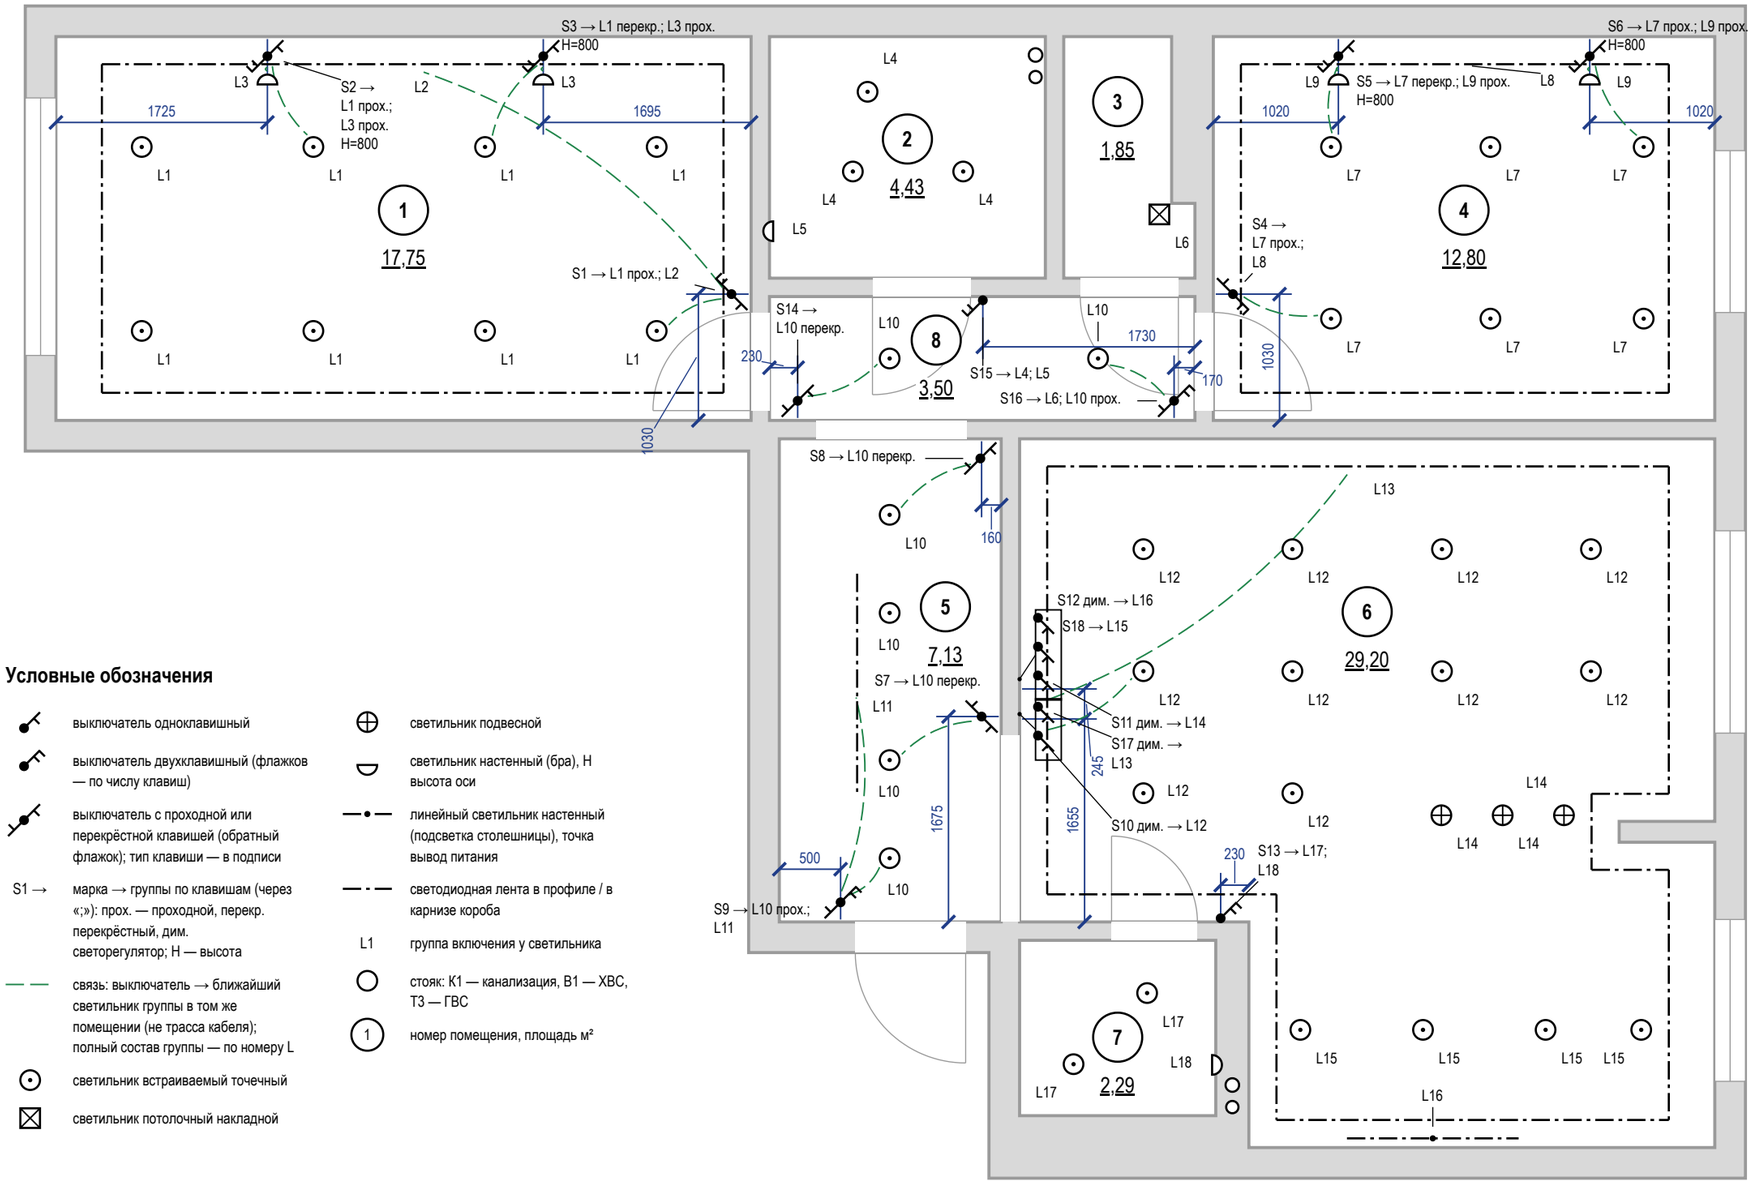

Условные обозначения

выключатель одноклавишный	светильник подвесной
выключатель двухклавишный (флажков — по числу клавиш)	светильник настенный (бра), H высота оси
выключатель с проходной или перекрёстной клавишей (обратный флажок); тип клавиши — в подписи	линейный светильник настенный (подсветка столешницы), точка вывод питания
S1 → марка → группы по клавишам (через «;»): прох. — проходной, перекр. перекрёстный, дим. светорегулятор; H — высота	светодиодная лента в профиле / в карнизе короба
связь: выключатель → ближайший светильник группы в том же помещении (не трасса кабеля); полный состав группы — по номеру L	L1 группа включения у светильника
светильник встраиваемый точечный	стояк: К1 — канализация, В1 — ХВС, Т3 — ГВС
светильник потолочный накладной	1 номер помещения, площадь м²

Примечания


1. За отметку 0,000 принят уровень чистого пола. Высоты H — от чистого пола до оси изделия; привязки — от чистовой грани стены до оси механизма (у рамки на несколько постов — до оси рамки).
2. Высота установки, не указанная на плане: выключатели — 900 мм от чистого пола (у кровати и другие — H у марки), со стороны дверной ручки (ПУЭ 7.1.51).
3. Какой выключатель какие светильники включает — по номеру группы L: у выключателя (S1 → L1; L2 — клавиши по порядку) и у каждого светильника. Пунктир подсказка к ближайшему светильнику группы в том же помещении (не дальше 3 м), это не трасса кабеля; выключатель за стеной (у двери санузла) и далёкая группа — только номер группы.
4. Группы из нескольких мест (L1 — S1, S2, S3; L3 — S2, S3; L7 — S4, S5, S6; L9 — S5, S6; L10 — S7, S8, S9, S14, S16): на крайних местах — проходные клавиши, на промежуточных — перекрёстные; механизмы — в ведомости изделий.
5. Светорегулятор — по заднему фронту (для LED-драйверов), совместимость с драйверами проверить до закупки.
6. Розеточные и мокрые линии — через УЗО или дифавтомат с током утечки не более 30 мА (ПУЭ 7.1.79); в санузле выполнить ДСУП (ПУЭ 7.1.87–7.1.88).
7. Кабель — медный, исполнение нг(А)-LS (ГОСТ 31565-2012); скрытая прокладка только горизонтально и вертикально, фактические трассы зафиксировать исполнительной схемой до закрытия отделкой.
8. Расчёт нагрузок, токов КЗ, селективности и сечений — по проекту ЭОМ организации с допуском СРО; лист задаёт состав, расположение и группы.

	Лист	№ док.	Подпись	Дата
Дизайнер	Кырлан А.С.			04.11.26

Проект: Трёхкомнатная квартира — **М 1:50**

Управление светильниками

Стадия	Лист	Листов
П	39	92

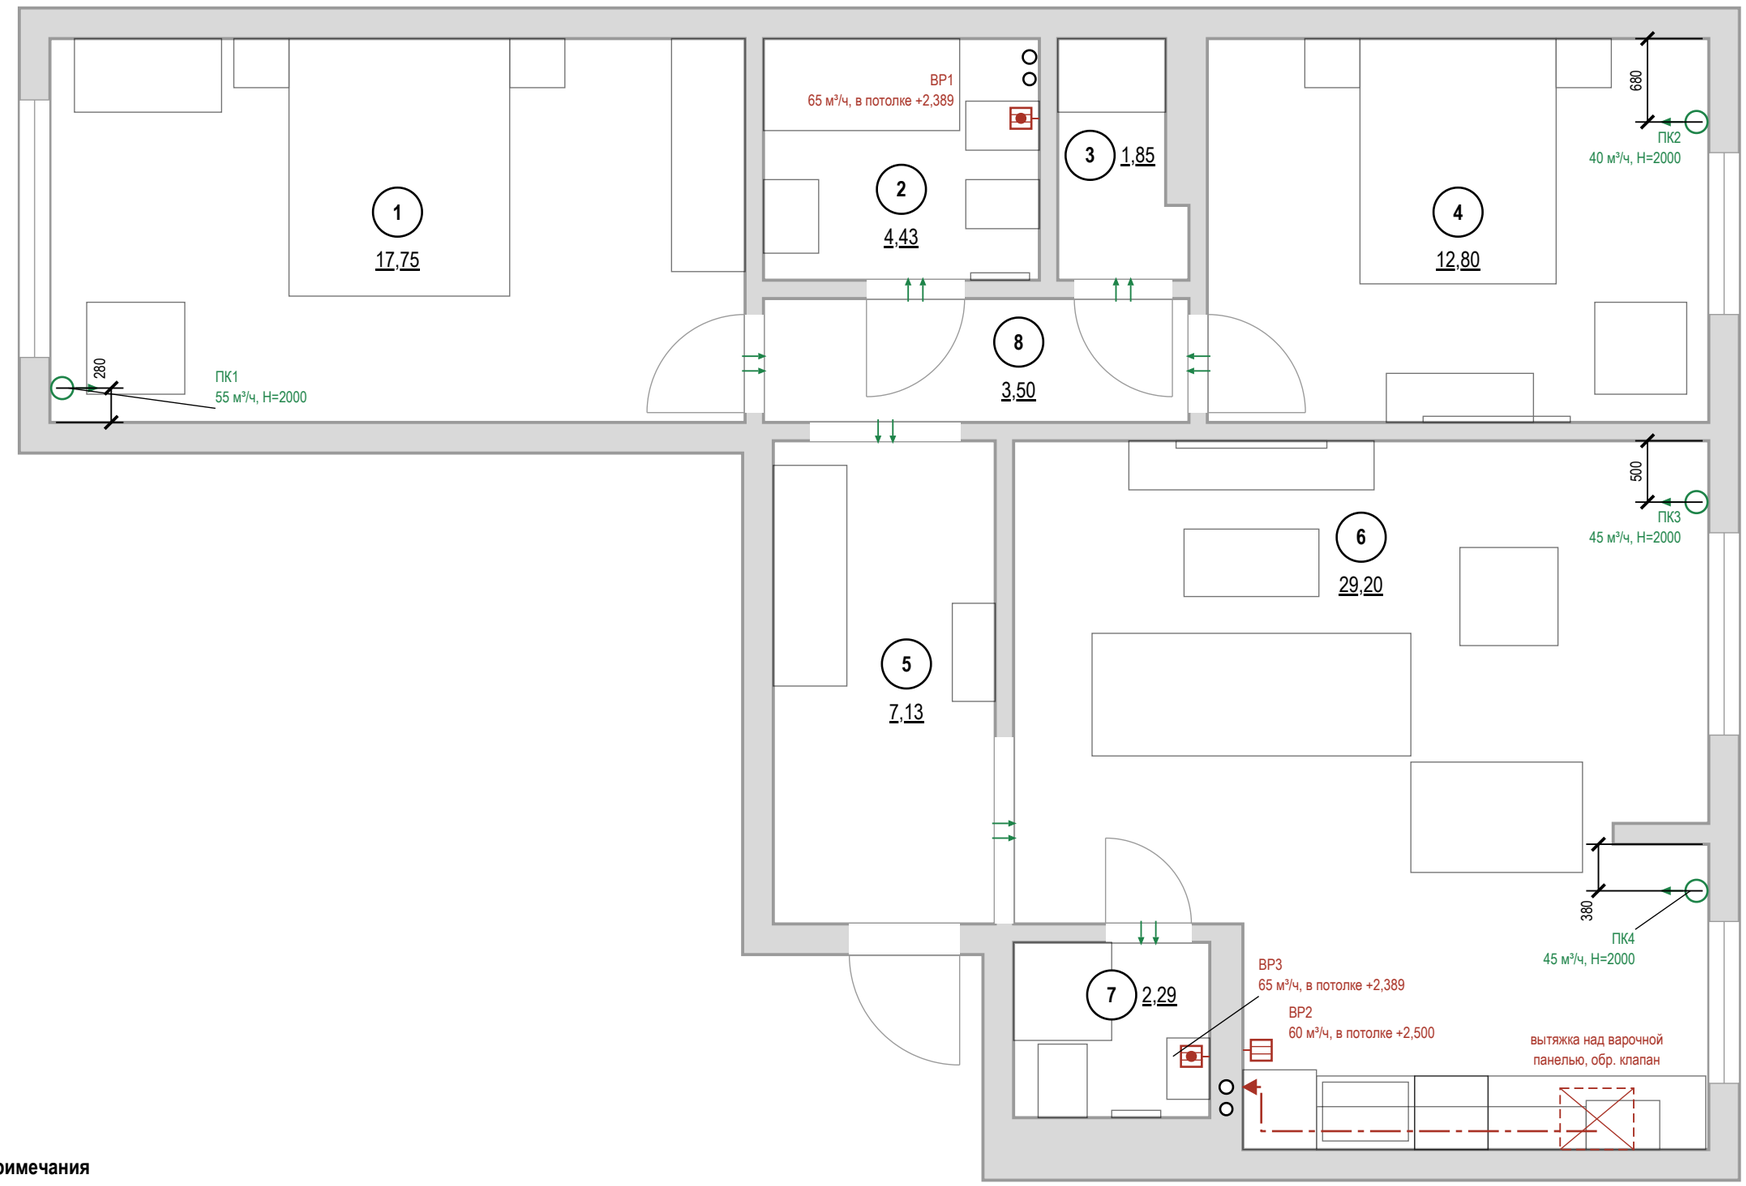

Условные обозначения

- стояк: К1 — канализация, В1 — ХВС, Т3 — ГВС
- номер помещения, площадь м²
- вытяжная решётка в подшивном потолке, воздуховод за потолком до канала
- вентилятор с обратным клапаном в подшивном потолке, воздуховод за потолком до канала
- приточный клапан (КИВ) в наружной стене: марка, расход, Н центра
- переток: зазор под полотном или переточная решётка
- кухонная вытяжка над варочной панелью
- воздуховод кухонной вытяжки в коробе под потолком
- отдельный вход воздуховода в вентканал, обратный клапан

Воздухообмен, м³/ч

№	Помещение	Выт. норма	Выт. проект	Прит. норма	Прит. проект	Устрой-ства
1	Спальня 1			54	55	ПК1
2	Ванная	50	65			ВР1
3	Гардеробная	1				переток
4	Спальня 2			39	40	ПК2
6	Кухня-гостиная	60	60	88	90	ВР2, ПК3, ПК4
7	Санузел 2	50	65			ВР3
	Итого	**161**	**190**	**181**	**185**	

Воздухообмен квартиры — по большей из сумм притока и вытяжки: норма 181 м³/ч, проект 190 м³/ч.
Вытяжка не меньше притока — баланс сведён.

Привязки — до обмера
Вентканалы в исходных данных не заданы: решётки и вход вытяжки показаны у стояков К1 (вентблок у мокрой зоны). До черновых работ — обмер каналов и проверка тяги; лист перевыпустить по факту.

Примечания

1. Расчёт систем ОВ и подбор оборудования — проектная организация с допуском СРО; лист даёт места, трассы и привязки.
2. Нормы вытяжки — СП 54.13330.2022 (Изм. 1, 2), табл. 7.1: кухня с электроплитой 60 м³/ч, с газовой 100; ванная и совмещённый санузел 50; уборная 25; гардеробная 0,2 ч⁻¹. Приток в жилые — 3 м³/ч на 1 м² (менее 20 м² общей площади на человека), иначе 30 м³/ч на человека.
3. Вентканалы и шахты не сужать, не переносить и не закрывать; вентилятор и кухонная вытяжка — через обратный клапан, без перекрытия естественной тяги.
4. Проектные расходы — не ниже нормы, вытяжка сведена с притоком вентиляторами мокрых помещений. Клапаны — в простенке у окна, центр 2000 мм, не над кроватью, не ближе 300 мм к стоякам отопления; типоразмер — на расход.
5. Под подшивным потолком вытяжка — в потолке, воздуховодом за потолком до канала. Кухонная вытяжка в воздухообмен не включена: воздуховод не менее Ø125 в коробе, вход в канал отдельный.
6. Переток — зазор под полотнами межкомнатных дверей или переточная решётка.
7. Кондиционирование заданием не предусмотрено; при установке трассы фреона и дренажа (не менее 40 мм/м, в К1 через сифон) и питание заложить до черновых работ.
8. Привязки оборудования — по паспортам приобретённых моделей, до черновых работ.

	Лист	№ док.	Подпись	Дата
Дизайнер	Кырлан А.С.			04.11.26

Проект: Трёхкомнатная квартира — **М 1:50**

План вентиляции

Стадия	Лист	Листов
П	40	92



Условные обозначения

- (1) — номер помещения, площадь м²
- радиатор отопления (марка РО-N, длина по плану)
- (T) — клапан с термоголовкой на подаче
- стояк отопления, подающий (Ст Т1-N)
- стояк отопления, обратный (Ст Т2-N)
- Т1 — отопление, подающий трубопровод
- Т2 — отопление, обратный трубопровод

Ведомость радиаторов

Марка	Помещение	Тип	Д×В×Г, мм	Низ / стена	Q, Вт
РО-1	1. Спальня 1	панельный	1400×600×100	120 / 40	расч.
РО-2	4. Спальня 2	панельный	900×600×100	120 / 40	расч.
РО-3	6. Кухня-гостиная	панельный	1100×600×100	120 / 40	расч.
РО-4	6. Кухня-гостиная	панельный	900×600×100	120 / 40	расч.

тип и мощность — по теплотехническому расчёту
Низ — от чистого пола, стена — зазор до задней панели, мм.


Привязки — до обмера
Стояки отопления в исходных данных не заданы: показаны у откосов окон, подводки — принципиально. До черновых работ — обмер стояков и паспорта приборов; лист перевыпустить по факту.

Примечания

1. Расчёт системы отопления, теплопотерь и подбор приборов — проектная организация с допуском СРО; лист даёт места и привязки.
2. Тип, длина и мощность радиаторов — по теплотехническому расчёту; лист задаёт места, зазоры и подключение.
3. Радиаторы — под каждым окном жилых комнат и кухни, центр по оси проёма, длина 0,7 ширины окна (кратно 100); окончательно — по расчёту.
4. Зазоры радиатора: низ не менее 100 мм от чистого пола, верх не менее 100 мм до подоконника, 30–50 мм от стены до задней панели; центр по оси окна с допуском ±20 мм. Верх до подоконника — 180 мм.
5. Радиаторы не закрывать глухими коробами и мебелью; перенос и замена приборов в многоквартирном доме — переустройство, согласование с управляющей организацией (ЖК РФ ст. 25–26); вынос на лоджию запрещён.
6. Трубы отопления через межквартирные стены не прокладывать (СП 51.13330.2011, п. 9.19); через перекрытия и перегородки — в гильзах.
7. Привязки приборов и подводок — по паспортам приобретённых радиаторов и клапанов, до черновых работ.
8. До закрытия отделкой трубопроводы отопления испытать гидростатическим давлением с оформлением акта (СП 73.13330.2016, 7.2–7.3).

					Проект: Трёхкомнатная квартира — М 1:50
	Лист	№ док.	Подпись	Дата	
Дизайнер	Кырлан А.С.			04.11.26	План отопления

Стадия	Лист	Листов
П	41	92

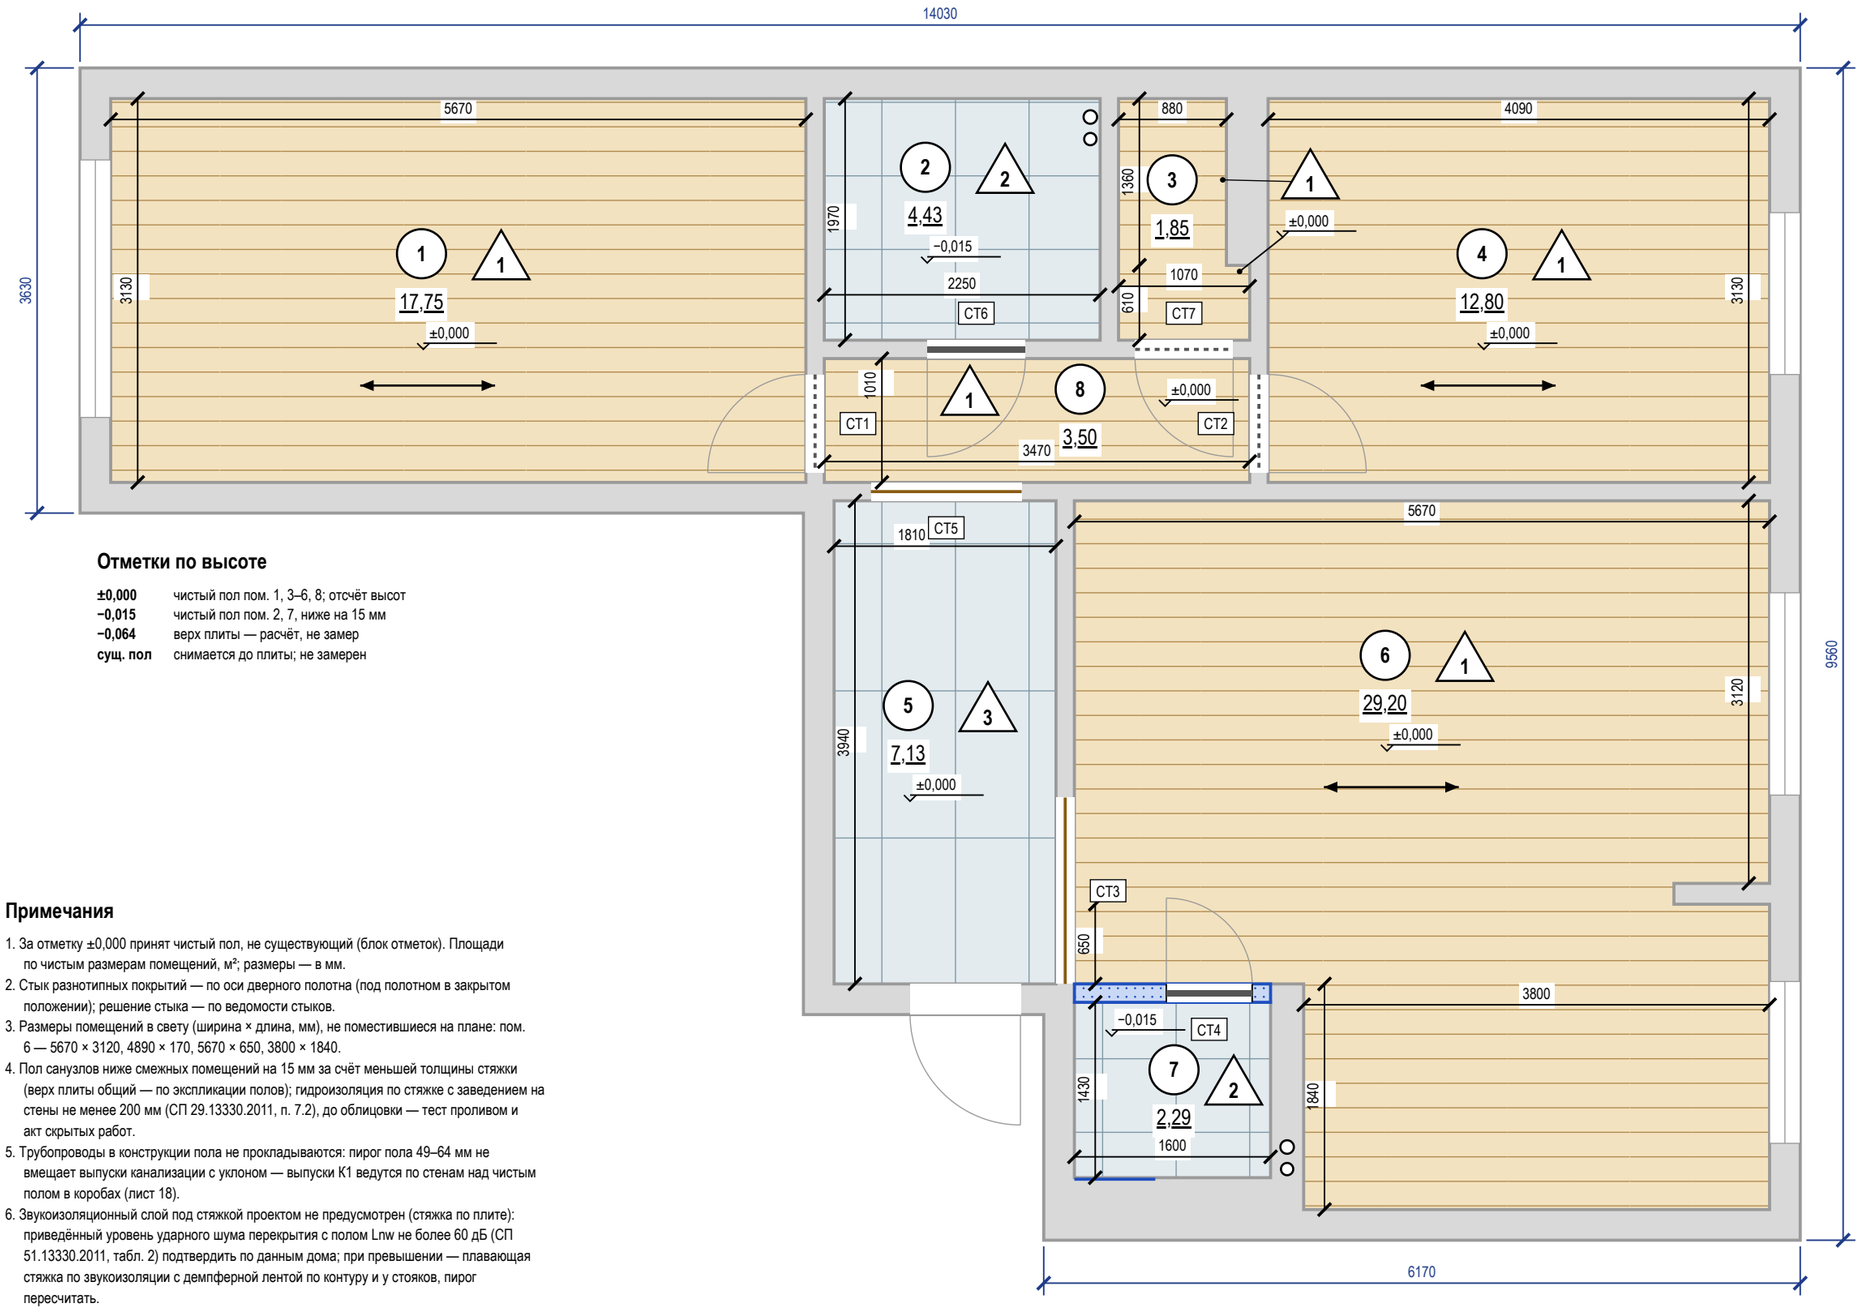




Отметки по высоте

±0,000	чистый пол пом. 1, 3–6, 8; отсчёт высот
−0,015	чистый пол пом. 2, 7, ниже на 15 мм
−0,064	верх плиты — расчёт, не замер
сущ. пол	снимается до плиты; не замерен

Примечания

1. За отметку ±0,000 принят чистый пол, не существующий (блок отметок). Площади по чистым размерам помещений, м²; размеры — в мм.
2. Стык разнотипных покрытий — по оси дверного полотна (под полотном в закрытом положении); решение стыка — по ведомости стыков.
3. Размеры помещений в свету (ширина × длина, мм), не поместившиеся на плане: пом. 6 — 5670 × 3120, 4890 × 170, 5670 × 650, 3800 × 1840.
4. Пол санузлов ниже смежных помещений на 15 мм за счёт меньшей толщины стяжки (верх плиты общий — по экспликации полов); гидроизоляция по стяжке с заведением на стены не менее 200 мм (СП 29.13330.2011, п. 7.2), до облицовки — тест проливом и акт скрытых работ.
5. Трубопроводы в конструкции пола не прокладываются: пирог пола 49–64 мм не вмещает выпуски канализации с уклоном — выпуски К1 ведутся по стенам над чистым полом в коробах (лист 18).
6. Звукоизоляционный слой под стяжкой проектом не предусмотрен (стяжка по плите): приведённый уровень ударного шума перекрытия с полом Lnw не более 60 дБ (СП 51.13330.2011, табл. 2) подтвердить по данным дома; при превышении — плавающая стяжка по звукоизоляции с демпферной лентой по контуру и у стояков, пирог пересчитать.
7. Штучные покрытия (инженерная доска): направление — по стрелке; влажность основания по СМ не более 2,0 % (по ТУ изготовителя).
8. Ровность основания — просвет под 2-метровой рейкой не более 2 мм: пом. 1, 3, 4, 6, 8 (инженерная доска), пом. 2, 5, 7 (керамогранит); проверить до укладки покрытия (СП 71.13330.2017, табл. 8.5).
9. Сетка на плитке — условная, в размер формата; точка старта и раскладка — по листу раскладки плитки.
10. Узор покрытия (заливка-код типа пола) прерывается под надписями — площадями помещений и отметками чистого пола.
11. Пироги полов — по экспликации полов: слои сверху вниз, толщины в мм; гидроизоляция мокрых зон — в пироге и в ведомости отделки; схема пола — без масштаба.

Экспликация полов

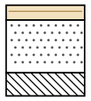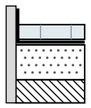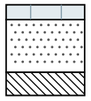Пом.	Тип пола	Схема пола	Элементы пола, толщина, мм	Площадь, м²
1, 3, 4, 6, 8	1		Инженерная доска на клею 14 Стяжка ЦПС М200 — 50 Плита перекрытия Всего 64 мм; ЧП ±0,000, верх плиты −0,064	65,10
2, 7	2		Керамогранит на клею С2 TE S1 — 14 Гидроизоляция обмазочная, 2 слоя, с заведением на стены 200 мм — 2 Стяжка ЦПС М200 — 33 Плита перекрытия Всего 49 мм; ЧП −0,015, верх плиты −0,064	6,72
5	3		Керамогранит на клею С2 TE S1 — 14 Стяжка ЦПС М200 — 50 Плита перекрытия Всего 64 мм; ЧП ±0,000, верх плиты −0,064	7,13
			Итого	**78,95**

Раскладка покрытий


Пом.	Укладка	Старт (оси от чистовых стен), мм	Отступ 1-го ряда / крайние плитки, мм
1	вдоль стен А/В, прямая	от стены А, 1-й ряд вдоль неё	зазор от стены не задан
2	прямая, сетка 600×600, шов 2	ось X 1101 от Г; ось Y 961 от А	X 498 / 498; Y 358 / 358
3	вдоль стен А/В, прямая	от стены А, 1-й ряд вдоль неё	зазор от стены не задан
4	вдоль стен А/В, прямая	от стены А, 1-й ряд вдоль неё	зазор от стены не задан
5	плитка	раскладка плиточника не задана	
6	вдоль стен А/В, прямая	от стены А, 1-й ряд вдоль неё	зазор от стены не задан
7	прямая, сетка 600×600, шов 2	ось X 776 от Г; ось Y 691 от А	X 474 / 474; Y 389 / 389
8	вдоль стен А/В, прямая	от стены А, 1-й ряд вдоль неё	зазор от стены не задан

Спецификация плинтусов


Наименование	Помещения	Длина, м (с запасом)
Плинтус МДФ под покраску 80×16, крепление к стене, окраска в цвет Farrow & Ball No. 241	1, 4, 5, 6, 8	72
Плинтус МДФ под покраску 80×16, крепление к стене, окраска в цвет Tikkurila V503	3	6

					Проект: Трёхкомнатная квартира — **М 1:50**
	Лист	№ док.	Подпись	Дата	
Дизайнер	Кырлан А.С.			04.11.26	План покрытий пола
					Стадия: П; Лист: 42; Листов: 92

Фрагмент 1. Ванная (пом. 2). Пол 600×600, шов 2 мм, М 1:20

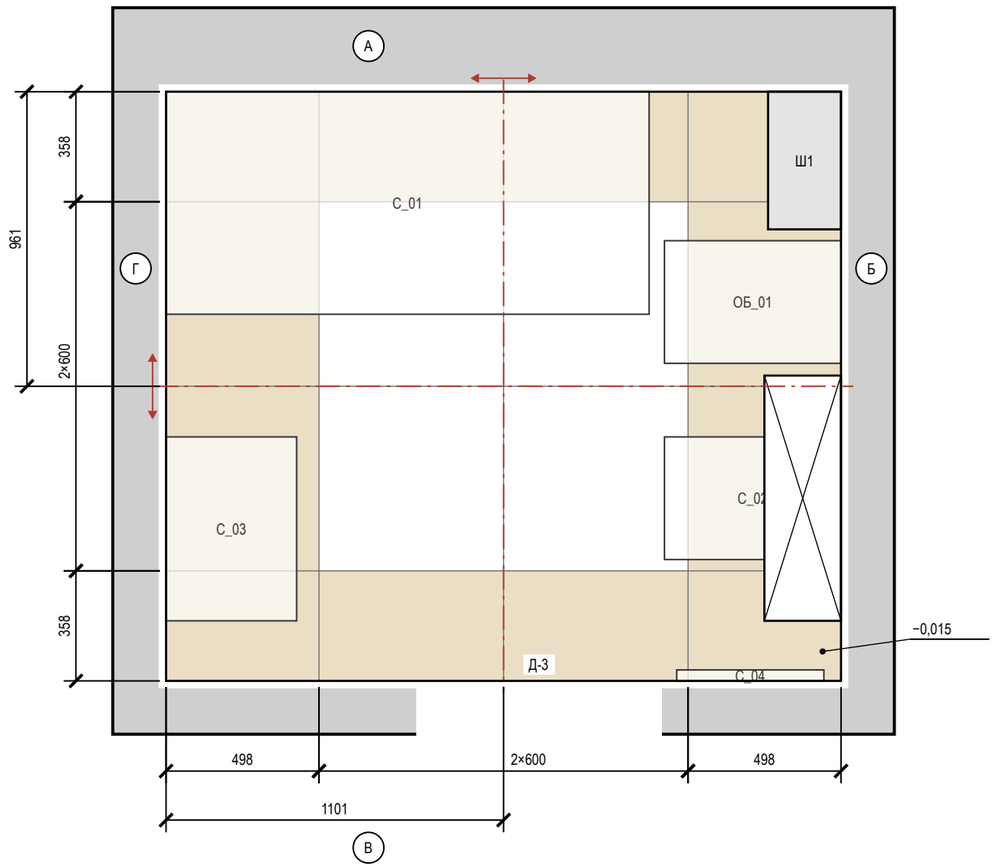

Фрагмент 2. Санузел 2 (пом. 7). Пол 600×600, шов 2 мм, М 1:20

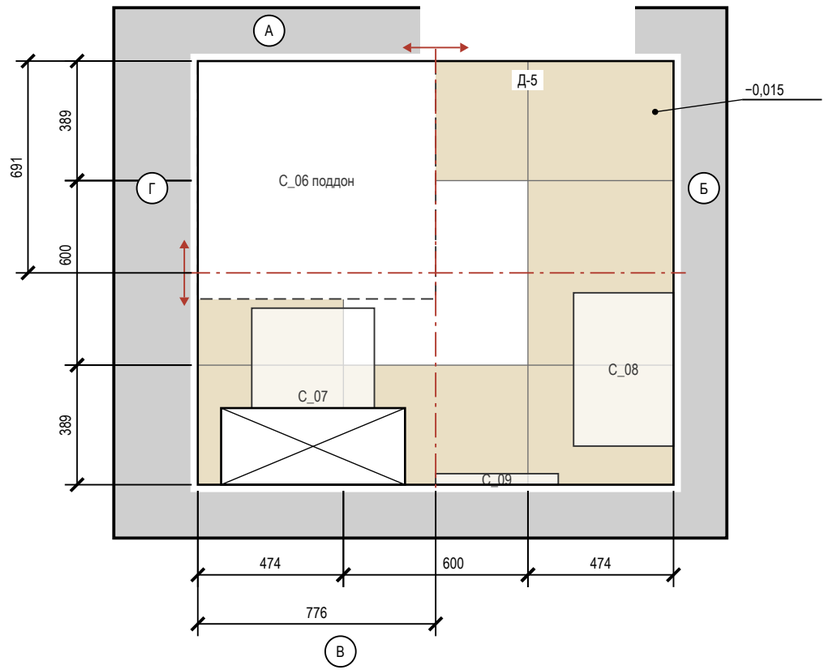

Примечания

1. Раскладка от чистовых размеров: стены санузлов теряют 10 + 5 + 9 = 24 мм на сторону (штукатурка, клей, плитка); подрезки — чистые, без шва.
2. Старт — от центра помещения (штрихпунктир, стрелки направление укладки); размер старта — от чистовых стен Г и А.
3. Раскладка пола «Прихожая» и фартука «Кухня-гостиная» на листе «Раскладка плитки. Прихожая. Фартук кухни».
4. Калибр партии не задан — до укладки замерить (рабочий размер W, ГОСТ 13996-2019) и пересчитать подрезки.
5. Количество: целые по раскладке + по одной на подрезку, запас 10 %; один артикул — одна партия и тон. Исключены поддон, короб, проёмы и места за коробом; S — по чистым граням: стены нетто = зона облицовки по ведомости отделки − место за коробом инсталляции 3,33 м² (плитку за коробом не кладут), короб — отдельной строкой.
6. Клей C2 TE S1 Ceresit CM 17; C2 TE S1 (ГОСТ Р 56387-2018), затирка CG2WA Mapei Ultracolor Plus 132; CG2WA; расход — по ТУ выбранной марки.
7. Гидроизоляция: пол и стены 200 мм от ЧП; над ванной до 2000 и 300 мм за борт (пом. 2), у душа — до 2000 и 500 мм за поддон (пом. 7) (см. развёртки); акт скрытых работ, пролив 24 ч.
8. Швы пола совмещены со швами стены А; по периметру демпферная лента.
9. Отметка чистого пола −0,015, порог 15 мм; стык с соседним покрытием — по оси полотна двери.

Ведомость материалов

Материал	Класс, код	Норма расхода	Кол-во
Затирка	CG2WA Mapei Ultracolor Plus 132	(a+b)/ab·шов·t·1,6	3,1 кг
Затирка	CG2WA	(a+b)/ab·шов·t·1,6	0,7 кг
Клей	C2 TE S1 Ceresit CM 17	1,5 кг/м²·мм, слой 5	311 кг (13 меш.)
Клей	C2 TE S1	1,5 кг/м²·мм, слой 5	73 кг (3 меш.)
Гидроизоляция	обмазочная, 2 слоя: пол, стены по периметру и зоны замачивания	по ТУ	20,0 м²
Демпф. лента	по периметру пола из плитки		22,4 м

Ведомость плитки


Помещение, поверхность	Плитка, код	Формат	Шов	S, м²	Целых	Подр.	С запасом
Ванная, пол	аналог: керамогранит под травертин	600×600	2	4,43	4	12	18
Ванная, стены А–Г	аналог: керамогранит под травертин	600×1200	2	16,00	9	20	33
Ванная, короб стояков Ш1 248×459	аналог: керамогранит под травертин	600×1200	2	1,65	0	4	6
Ванная, короб инсталляции	аналог: керамогранит под травертин	600×1200	2	1,76	0	6	7
Санузел 2, пол	аналог: керамогранит под травертин	600×600	2	2,29	0	8	9
Санузел 2, стены А–Г	аналог: керамогранит под травертин	600×1200	2	12,38	5	19	28
Санузел 2, короб инсталляции	аналог: керамогранит под травертин	600×1200	2	1,47	1	3	5
Прихожая, пол	аналог: керамогранит ректифицированный под травертин, матовый	600×1200	2	7,13	2	10	14
Кухня-гостиная, фартук (ст. В)	аналог: керамогранит под травертин, матовый	1200×600	2	1,85	0	4	5
Итого 600×600				6,72	4	20	27
Итого 600×1200				**42,24**	**17**	**66**	**98**

Условные обозначения


- плитка целая; тонкая линия — шов
- плитка с подрезкой (размер — на цепочке)
- ось старта; стрелки — направление укладки
- сантехприбор: габарит, высота по практике
- поддон душа — плитку пола под ним не кладут
- короб инсталляции: плитка пола — до короба
- короб стояков (Ш…): плитка пола — до короба
- отметка чистого пола на полке выноски, м
- (А) обозначение стены А–Г (как на развёртках)

					Проект: Трёхкомнатная квартира	М 1:20
	Лист	№ док.	Подпись	Дата		
Дизайнер	Кырлан А.С.			04.11.26	Раскладка плитки. Планы полов	Стадия: П; Лист: 43; Листов: 92

Фрагмент 1. Прихожая (пом. 5). Пол 600×1200, шов 2 мм, М 1:20

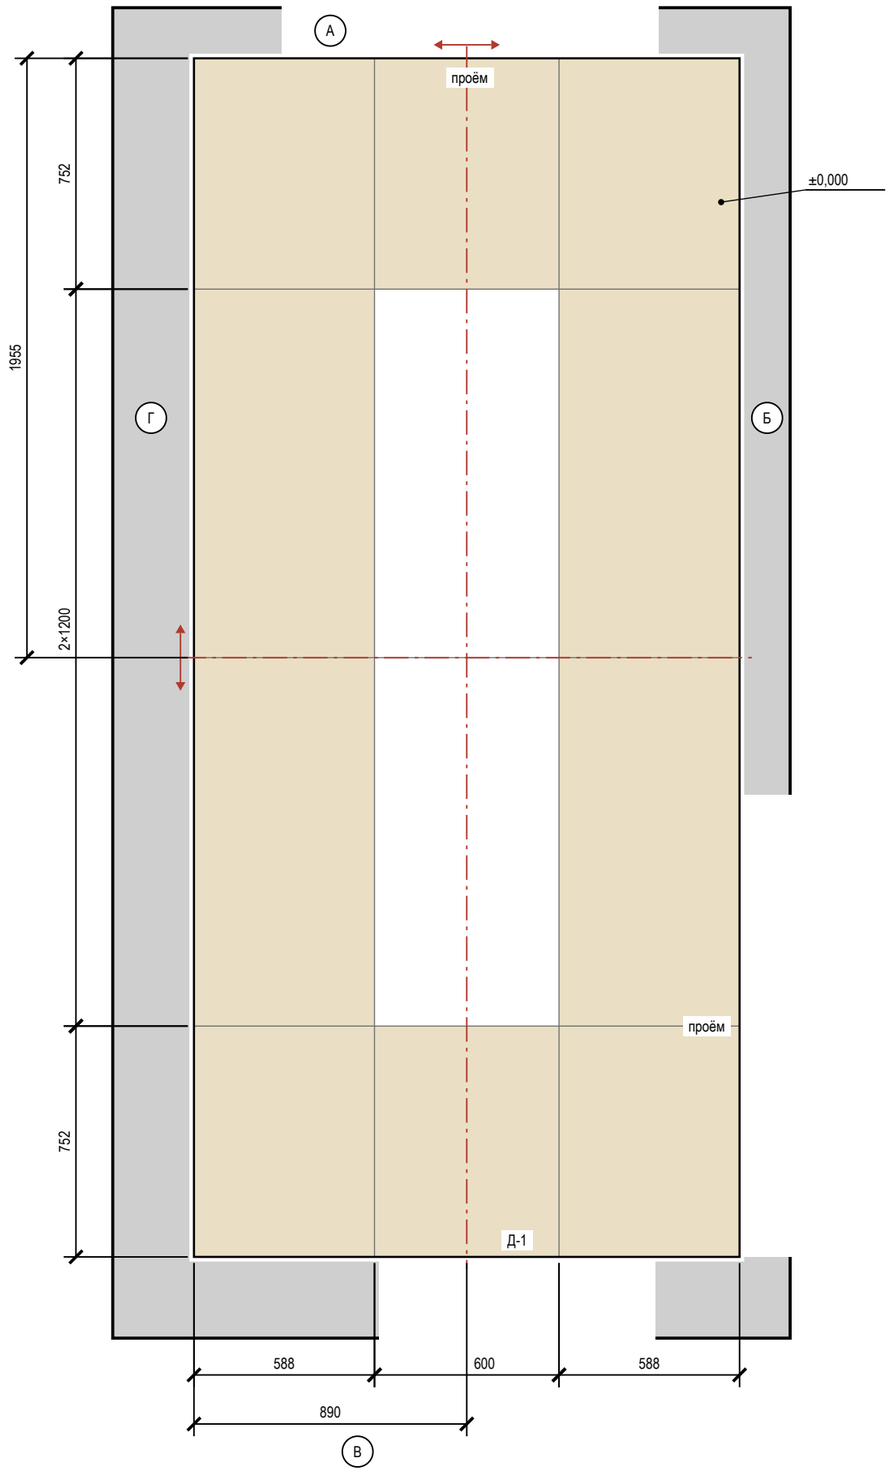

Фрагмент 2. Кухня-гостиная (пом. 6), фартук, стена В. 1200×600, шов 2 мм, М 1:20

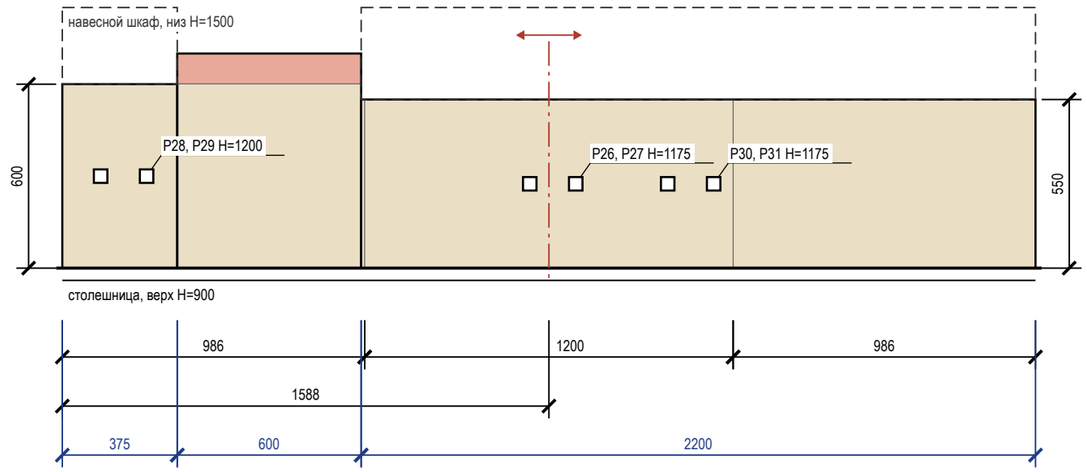

Условные обозначения

- плитка целая; тонкая линия — шов
- плитка с подрезкой (размер — на цепочке)
- ось старта; стрелки — направление укладки
- электроточка: марка и H — по листам ЭОМ
- столешница (верх)
- навесной шкаф над фартуком
- отметка чистого пола на полке выноски, м
- (А) обозначение стены А–Г (как на развёртках)

Подсчёт плитки


Поверхность	Формат	S, м²	Целых	Подр.	С запасом
Прихожая, пол	600×1200	7,13	2	10	14
Кухня-гостиная, фартук (ст. В)	1200×600	1,85	0	4	5

Примечания

1. Прихожая: керамогранит 600×1200, длинная сторона — вдоль стен Б и Г, шов 2 мм, прямая раскладка от центра. Стены окрашены: раскладка от чистового контура минус штукатурка и шпаклёвка 15 мм на сторону (принято); подрезки 588 / 752 мм, срез — под плинтус.
2. Прихожая: деформационный зазор по периметру 8–10 мм под плинтусом; в проёмах — стык с соседним покрытием по оси полотна двери. Клей C2 TE S1, затирка CG2WA.
3. Фартук, Кухня-гостиная: 1200×600 горизонтально, шов 2 мм; зоны 2200 мм — 900…1450, 600 мм — 900…1600, 375 мм — 900…1500 (от столешницы до низа навесного шкафа, без шкафа — 700 мм). Старт от центра участка, подрезки 986 мм. Площадь 1,85 м² — как в ведомости отделки.
4. Фартук — после монтажа столешницы, низ на 2–3 мм выше неё, шов со столешницей — санитарный герметик; навесные шкафы — после фартука. Торцы у пенала и стены — профиль или запил 45°.
5. Фартук, Кухня-гостиная: в зоне до отм. 1600 верхний ряд подрезан 98 мм — меньше 1/3 плитки; полоса прикрыта корпусом навесного модуля и на виду не остаётся. Раскладкой не снимается: убрать подрезку можно, только выровняв низ этого модуля с соседними (1450 мм) — решение мебельщика.
6. Клей, затирка и итог по форматам — в ведомостях листа «Раскладка плитки. Планы полов».


					Проект: Трёхкомнатная квартира — **М 1:20**
	Лист	№ док.	Подпись	Дата	
Дизайнер	Кырлан А.С.			04.11.26	Раскладка плитки. Прихожая. Фартук кухни
					Стадия: П; Лист: 44; Листов: 92

Развёртка стены А

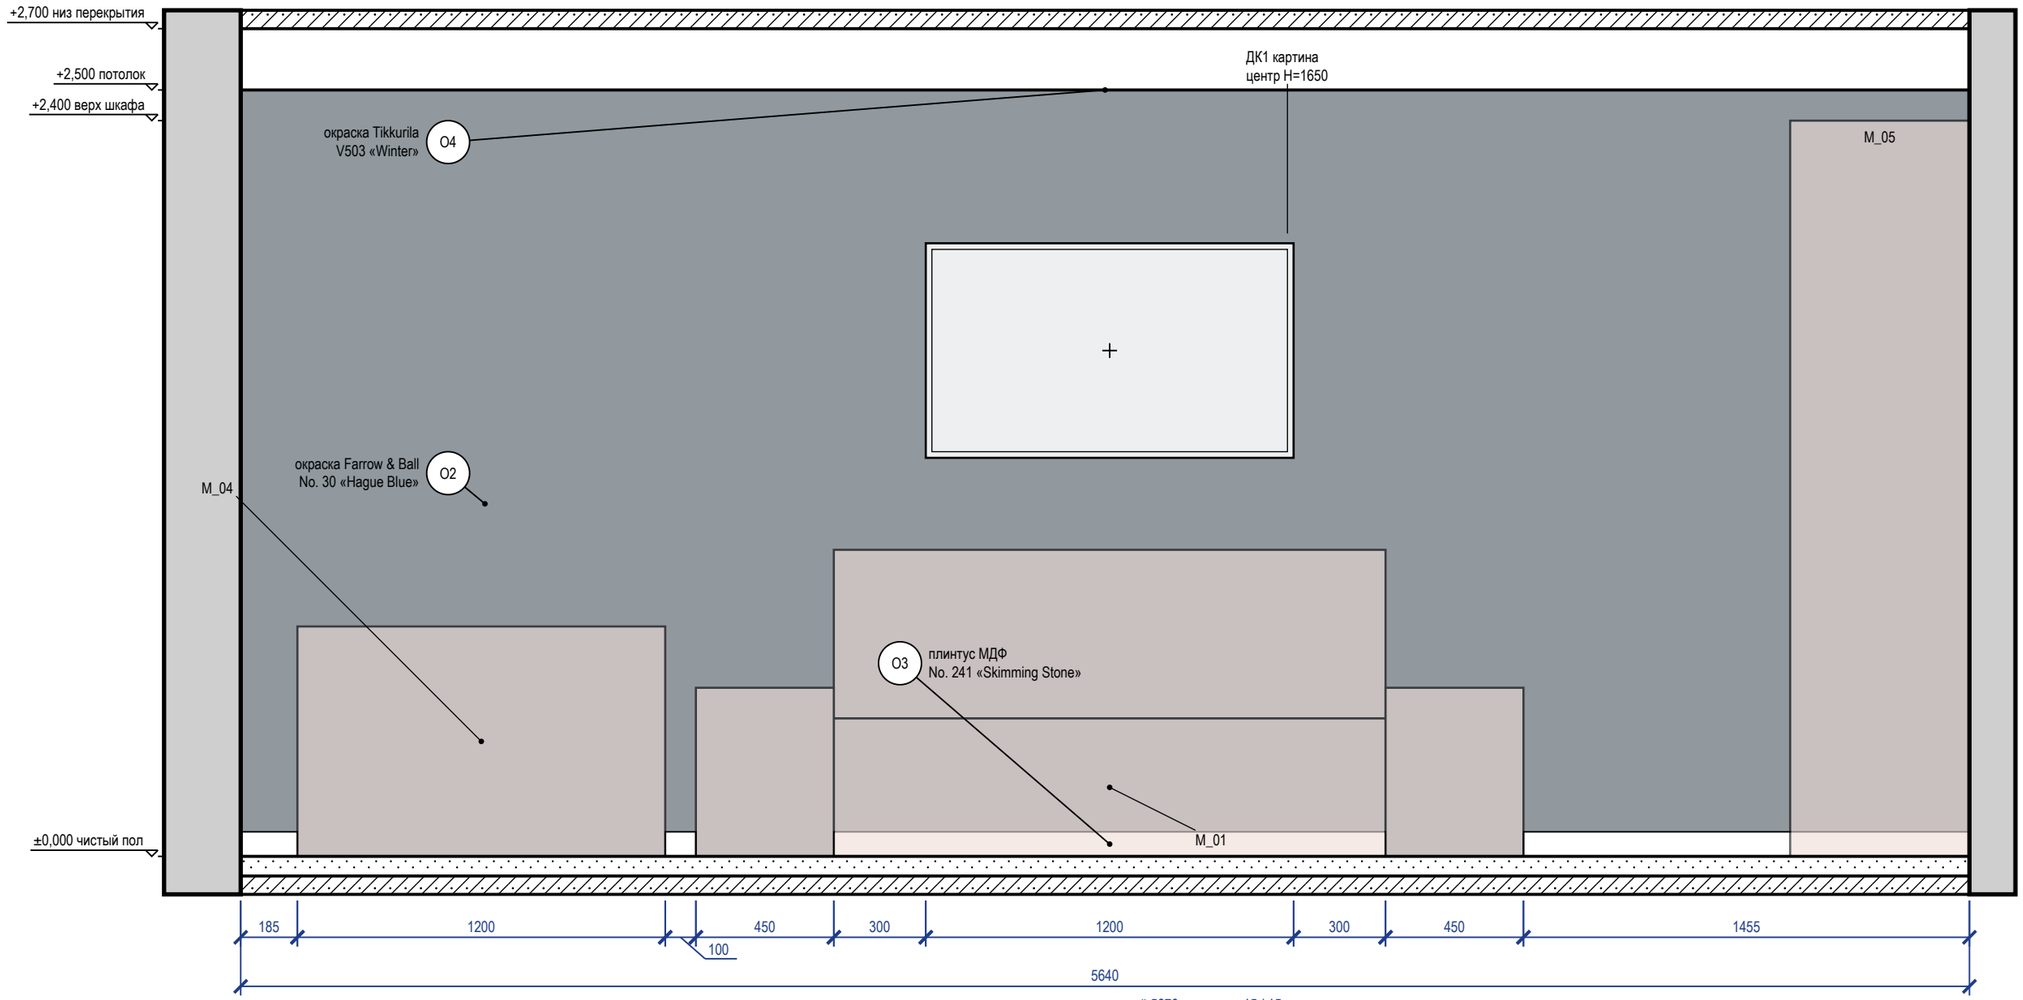

между чистовыми гранями: черновой 5670 − отделка 15 / 15

Схема развёрток (М 1:100)

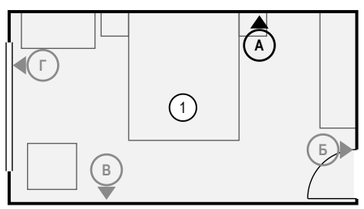

Ведомость отделки (на листе)

Марка	Поверхность	Материал, изделие	Цвет, код	Кол.
O2	акцентная стена	окраска, Farrow & Ball Modern Emulsion, матовая, подготовка Q3	Farrow & Ball No. 30 «Hague Blue»	14,1 м²
O3	плинтус	плинтус МДФ, h 80 мм, аналог: плинтус МДФ под покраску 80×16	Farrow & Ball No. 241 «Skimming Stone»	3,5 м
O4	потолок	окраска, Tikkurila Anti-Reflex 2, глубокоматовая, подготовка Q3	Tikkurila V503 «Winter»	17,8 м²

Примечания

1. Размеры — в мм от чистовых поверхностей стен; условные обозначения и общие указания — лист 3.
2. Стена А показана двумя видами: здесь — архитектурная развёртка (мебель, отделка, проёмы, высоты), электроточки и выводы ВК с привязками и таблицей — на листе 46 («Привязки»).
3. Картины и зеркала крепить к основанию по паспорту изделия (закладные и анкеры — в перечне скрытых работ); крест — ось центра предмета.
4. Потолок — у каждой стены свой, по плану потолков (ПТ1); ступени — зоной, кромка короба перед нишей — тонкой линией; в поле потолка: ПТ2 +2,600.

					Проект: Трёхкомнатная квартира	М 1:20
	Лист	№ док.	Подпись	Дата	Развёртка стены А. Спальня 1 (пом. 1)	Стадия: П; Лист: 45; Листов: 92
Дизайнер	Кырлан А.С.			04.11.26		

Развёртка стены А: электроточки и выводы

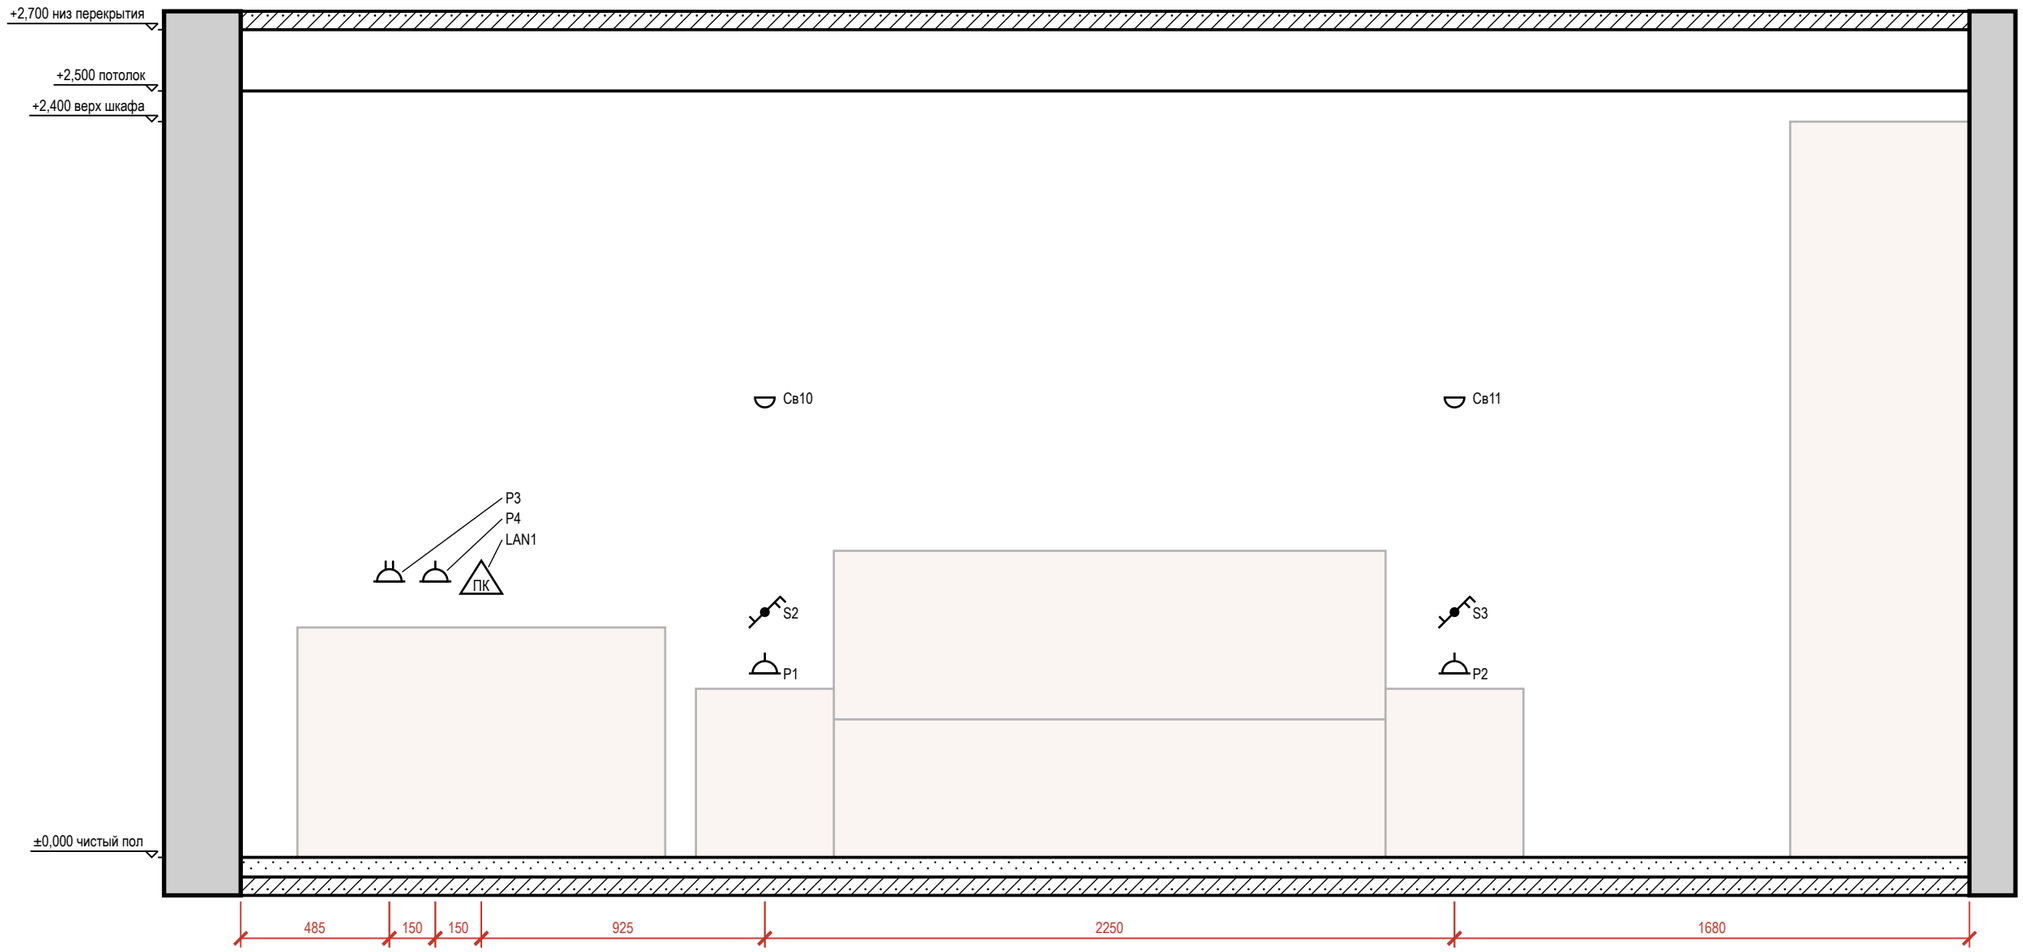



Таблица привязок электроточек и выводов

Марка	Назначение	От угла, мм	Н от пола, мм	Примечание
P3	розетка: рабочий стол	485	900	рамка 2 поста, гр. 4
P4	розетка: рабочий стол	635	900	гр. 4
LAN1	розетка RJ45: рабочий стол	785	900	
P1	розетка: у кровати	1710	600	гр. 4
S2	выключатель	1710	800	гр. 1
Св10	светильник настенный	1710	1500	гр. 1
P2	розетка: у кровати	3960	600	гр. 4
S3	выключатель	3960	800	гр. 1
Св11	светильник настенный	3960	1500	гр. 1

Условные обозначения

- розетка с заземляющим контактом; у знака — марка, ×N постов в рамке, гр. — группа щита, Н — высота оси, мм
- выключатель одноклавишный
- выключатель двухклавишный (флажков — по числу клавиш)
- выключатель с проходной или перекрёстной клавишей (обратный флажок); тип клавиши — в подписи
- светильник настенный (бра), Н — высота оси
- ПК — розетка компьютерная RJ45
- привязки точек и выводов от угла и от пола, мм
- А — марка развёртки: буква стены, стрелка — взгляд

Схема развёрток (М 1:100)

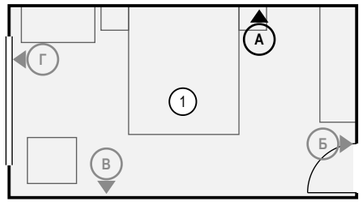

Примечания

1. Вид «Привязки» стены А — электроточки и выводы ВК; архитектурная развёртка (мебель, отделка, проёмы, высоты) — на листе 45. Мебель и приборы — подложкой для ориентира; их марки и обозначения мебели, проёмов и стен — там же.
2. Привязки — в мм: по горизонтали от левого чистового угла стены до оси изделия, Н — от чистого пола до оси; все точки — в таблице привязок. Красная цепочка — привязки по осям; точки ближе 120 мм одна к другой в цепочку не дробятся — их привязки только в таблице.
3. У знака — марка электроточки (Р — розетка, S — выключатель, Св — светильник, ЭВ — вывод кабеля); условные обозначения и общие указания — лист 3.

					Проект: Трёхкомнатная квартира — М 1:20
	Лист	№ док.	Подпись	Дата	
Дизайнер	Кырлан А.С.			04.11.26	Привязки электроточек, стена А. Спальня 1 (пом. 1)

Стадия	Лист	Листов
П	46	92

Развёртка стены Б


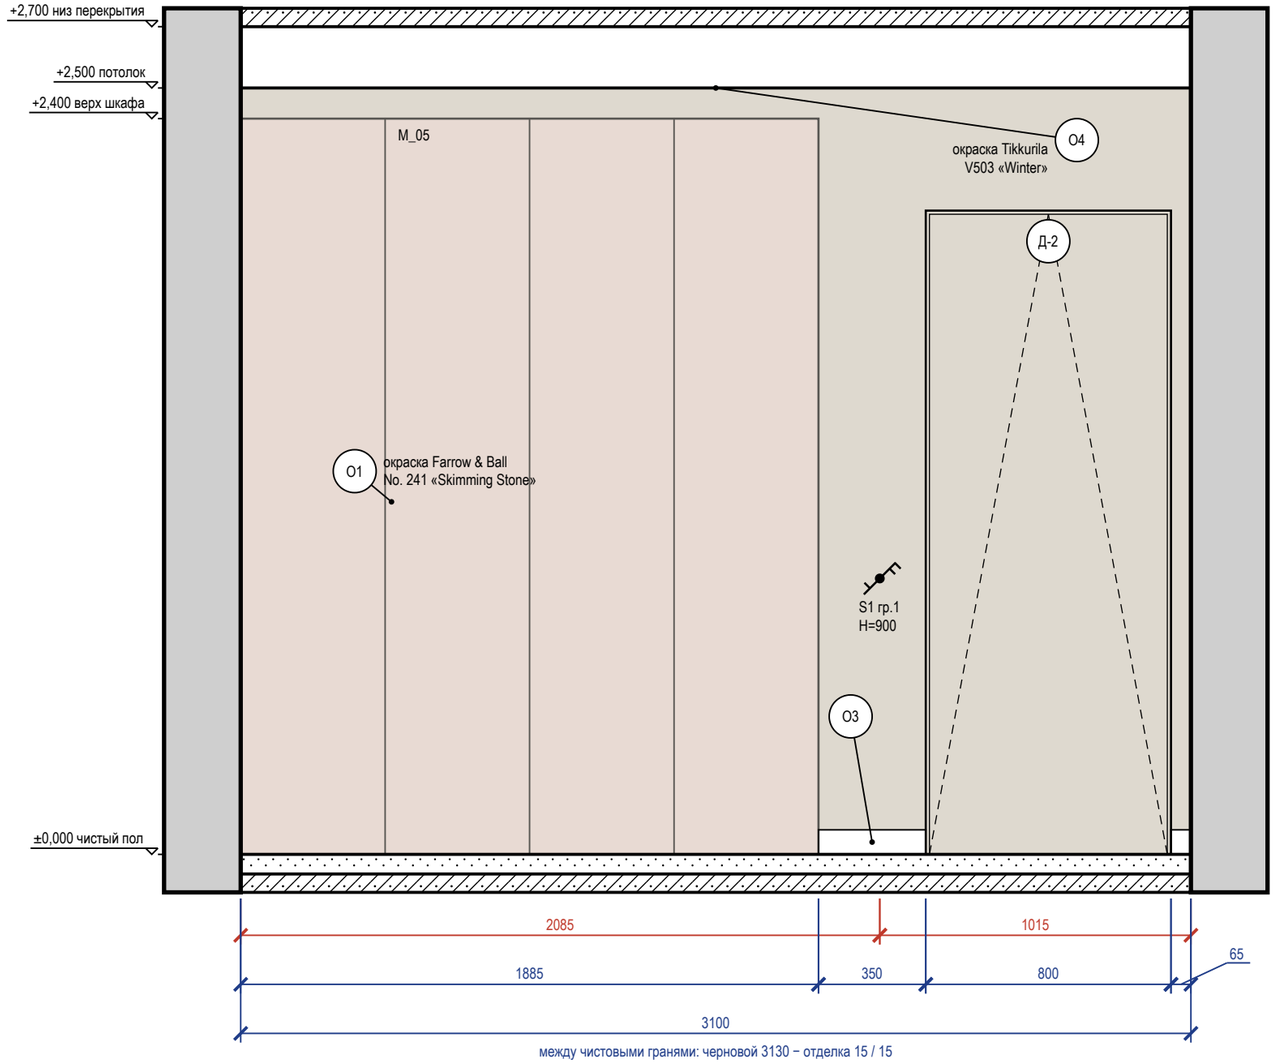


Схема развёрток (М 1:100)

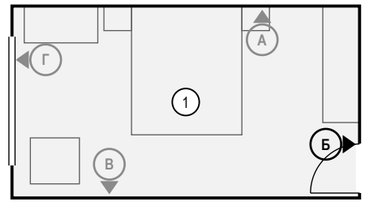

Ведомость отделки (на листе)

Марка	Поверхность	Материал, изделие	Цвет, код	Кол.
О1	стены	окраска, Farrow & Ball Modern Emulsion, матовая, подготовка Q3	Farrow & Ball No. 241 «Skimming Stone»	6,1 м²
О3	плинтус	плинтус МДФ, h 80 мм, аналог: плинтус МДФ под покраску 80×16	Farrow & Ball No. 241 «Skimming Stone»	0,4 м
О4	потолок	окраска, Tikkurila Anti-Reflex 2, глубокоматовая, подготовка Q3	Tikkurila V503 «Winter»	17,8 м²

Примечания

1. Размеры — в мм от чистовых поверхностей стен; условные обозначения и общие указания — лист 3.
2. Двери скрытого монтажа — полотно в плоскости стены, отделка стены по полотну, плинтус прерывается у короба (узел — на листе узлов).
3. Потолок — у каждой стены свой, по плану потолков (ПТ1); ступени — зоной, кромка короба перед нишей — тонкой линией; в поле потолка: ПТ2 +2,600.

					Проект: Трёхкомнатная квартира — М 1:20
	Лист	№ док.	Подпись	Дата	Развёртка стены Б. Спальня 1 (пом. 1)
Дизайнер	Кырлан А.С.			04.11.26	

Стадия	Лист	Листов
П	47	92

выпуск 04.11.2026 № 503a52061a · стр. 47 из 92

Развёртка стены В


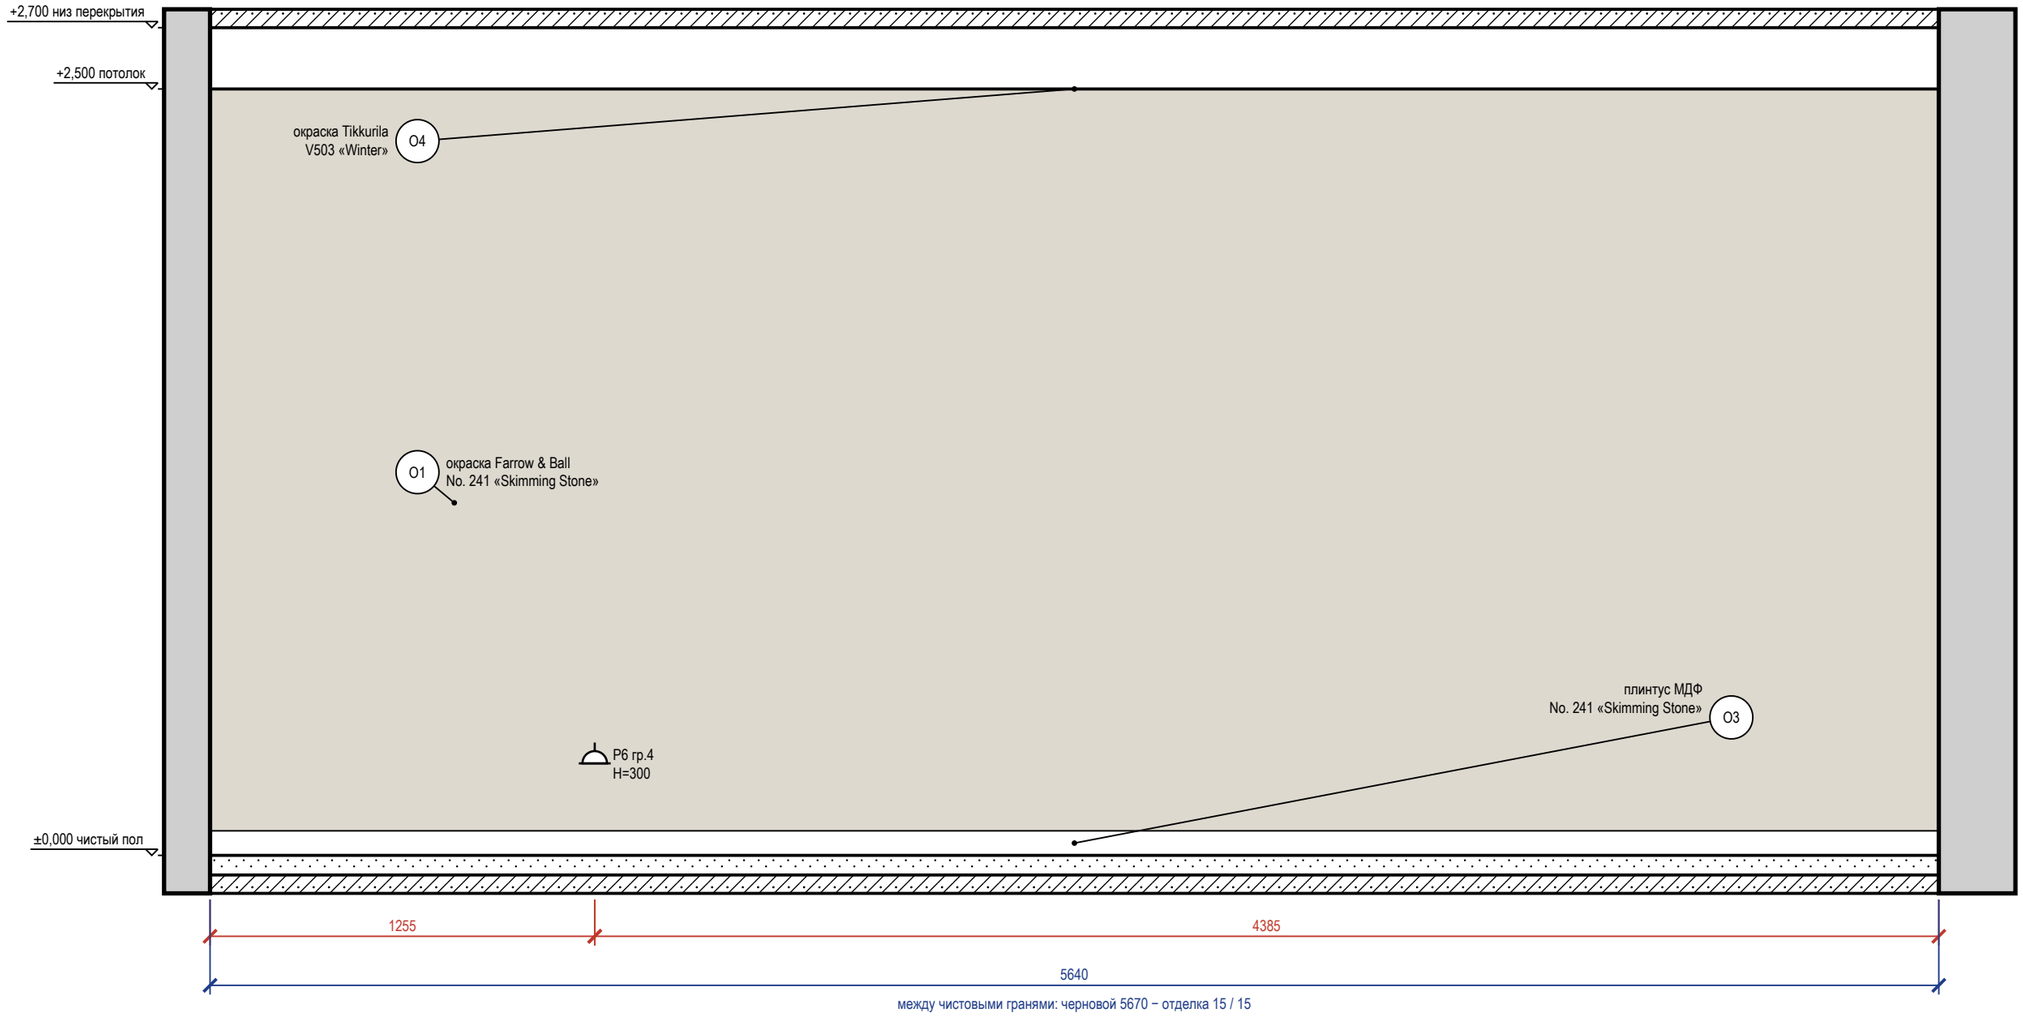


Схема развёрток (М 1:100)

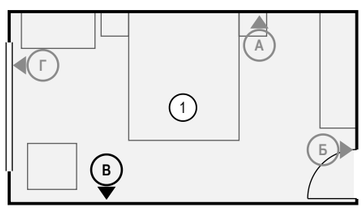

Ведомость отделки (на листе)

Марка	Поверхность	Материал, изделие	Цвет, код	Кол.
O1	стены	окраска, Farrow & Ball Modern Emulsion, матовая, подготовка Q3	Farrow & Ball No. 241 «Skimming Stone»	14,1 м²
O3	плинтус	плинтус МДФ, h 80 мм, аналог: плинтус МДФ под покраску 80×16	Farrow & Ball No. 241 «Skimming Stone»	5,6 м
O4	потолок	окраска, Tikkurila Anti-Reflex 2, глубокоматовая, подготовка Q3	Tikkurila V503 «Winter»	17,8 м²

Примечания

1. Размеры — в мм от чистовых поверхностей стен; условные обозначения и общие указания — лист 3.
2. Потолок — у каждой стены свой, по плану потолков (ПТ1); ступени — зоной, кромка короба перед нишей — тонкой линией; в поле потолка: ПТ2 +2,600.

					Проект: Трёхкомнатная квартира — М 1:20
	Лист	№ док.	Подпись	Дата	Развёртка стены В. Спальня 1 (пом. 1)
Дизайнер	Кырлан А.С.			04.11.26	

Стадия	Лист	Листов
П	48	92

Развёртка стены Г


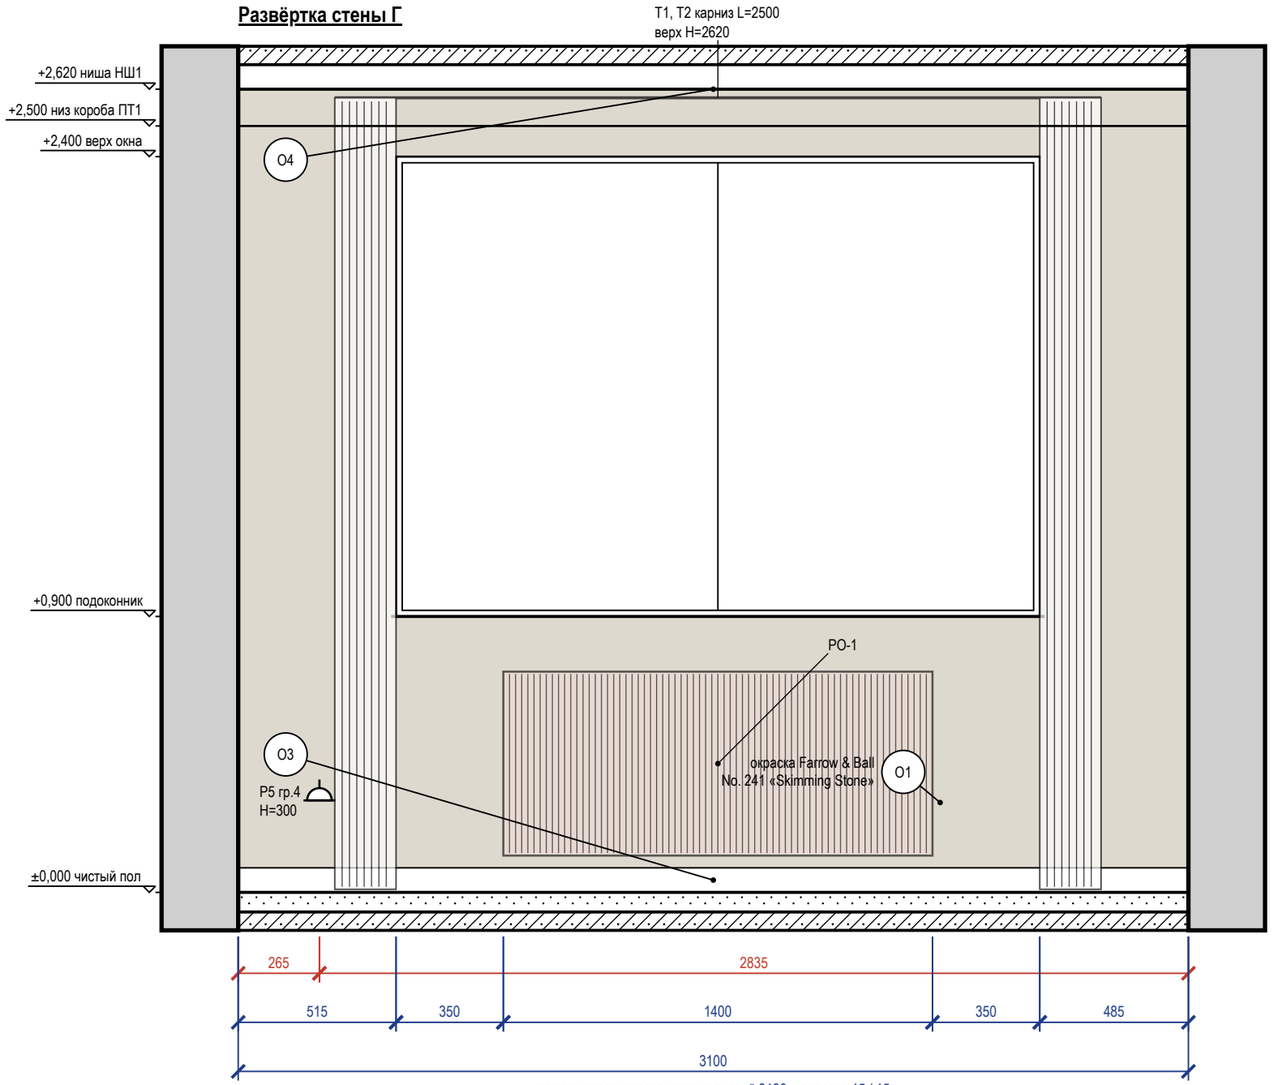


Схема развёрток (М 1:100)

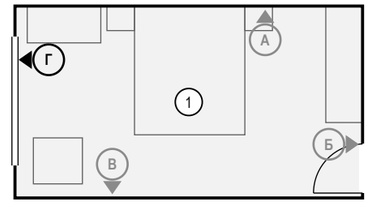

Ведомость отделки (на листе)

Марка	Поверхность	Материал, изделие	Цвет, код	Кол.
О1	стены	окраска, Farrow & Ball Modern Emulsion, матовая, подготовка Q3	Farrow & Ball No. 241 «Skimming Stone»	5 м²
О3	плинтус	плинтус МДФ, h 80 мм, аналог: плинтус МДФ под покраску 80×16	Farrow & Ball No. 241 «Skimming Stone»	3,1 м
О4	потолок	окраска, Tikkurila Anti-Reflex 2, глубокоматовая, подготовка Q3	Tikkurila V503 «Winter»	17,8 м²

Примечания

1. Размеры — в мм от чистовых поверхностей стен; условные обозначения и общие указания — лист 3.
2. Карнизы (шины) — по ведомости текстиля декоратора: длина L и верх H на развёртке — те же числа, что в ведомости; крепление — до окраски потолка.
3. Потолок — у каждой стены свой, по плану потолков (НШ1, ПТ1); ступени — зоной, кромка короба перед нишей — тонкой линией; в поле потолка: ПТ2 +2,600.


	Лист	№ док.	Подпись	Дата
Дизайнер	Кырлан А.С.			04.11.26

Проект: Трёхкомнатная квартира — **М 1:20**

Развёртка стены Г. Спальня 1 (пом. 1)

Стадия	Лист	Листов
П	49	92

Развёртка стены А

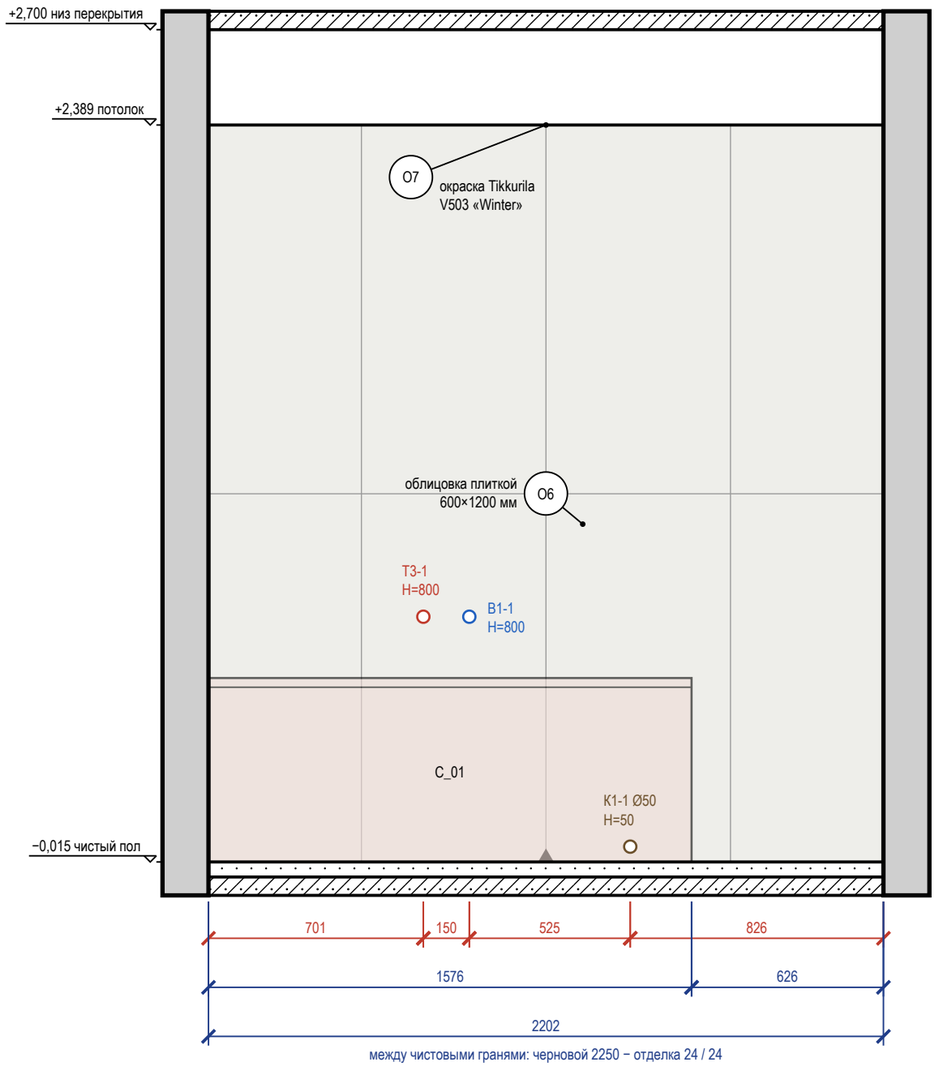

Развёртка стены Б


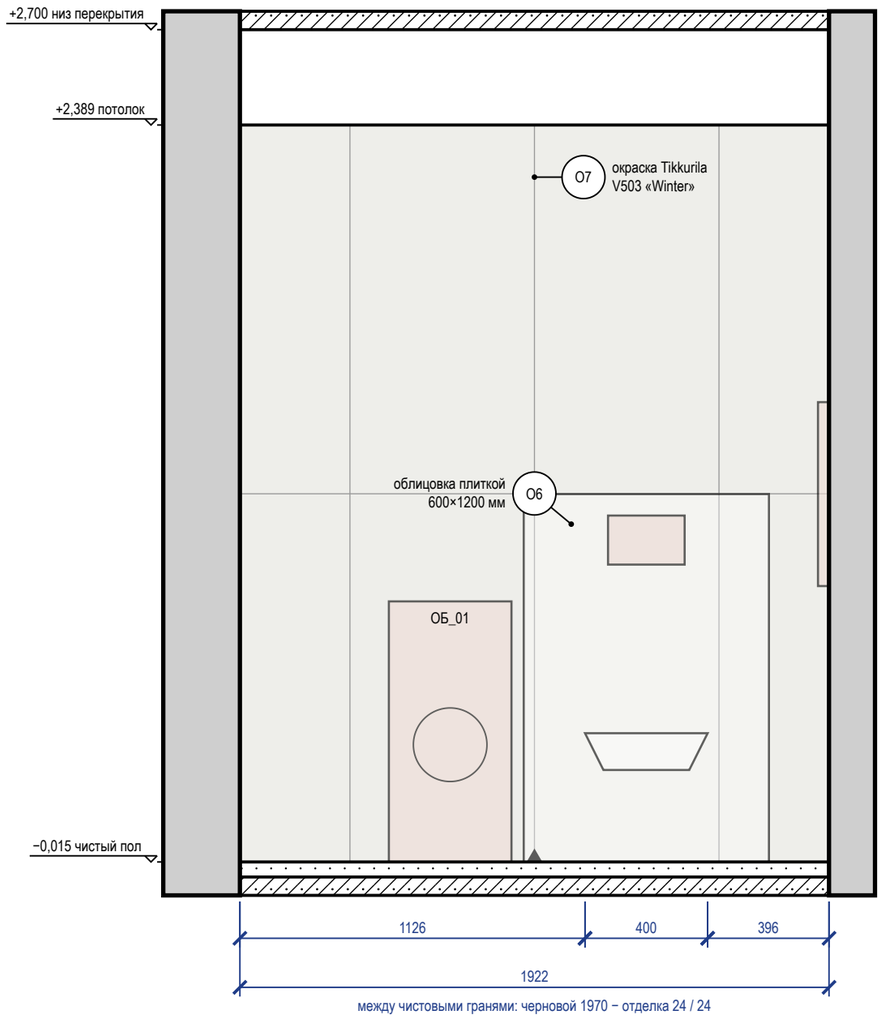


Схема развёрток (М 1:100)

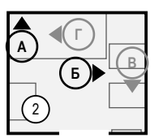

Ведомость отделки (на листе)


Марка	Поверхность	Материал, изделие	Цвет, код	Кол.
О6	стены	облицовка плиткой, 600×1200×9 мм, аналог: керамогранит под травертин, матовый, затирка CG2WA		9,9 м²
О7	потолок	окраска, Tikkurila Luja 7, матовая, подготовка Q3	Tikkurila V503 «Winter»	4,4 м²

Примечания

1. Размеры — в мм от чистовых поверхностей стен; условные обозначения и общие указания — лист 3.
2. Стена Б показана двумя видами: здесь — архитектурная развёртка (мебель, отделка, проёмы, высоты), электроточки и выводы ВК с привязками и таблицей — на листе 52 («Привязки»).
3. Схема мебели, приборов и декора не является технической документацией для производства мебели; габариты — по паспортам изделий.
4. Выводы ВК — коды и высоты по листу выводов сантехники.
5. Облицовка — по сетке швов 2 мм, раскладка от оси стены (треугольник у пола), целые ряды от пола; подрезки — по листу раскладки плитки.
6. Гидроизоляция в 2 слоя, заход на стены 200 мм; над ванной — до 2000 и 300 мм за борт — до облицовки, с актом скрытых работ и тестом проливом (узел — на листе узлов).


					Проект: Трёхкомнатная квартира	М 1:20
	Лист	№ док.	Подпись	Дата		
Дизайнер	Кырлан А.С.			04.11.26	Развёртки стен А, Б. Ванная (пом. 2)	Стадия: П; Лист: 50; Листов: 92

Развёртка стены В

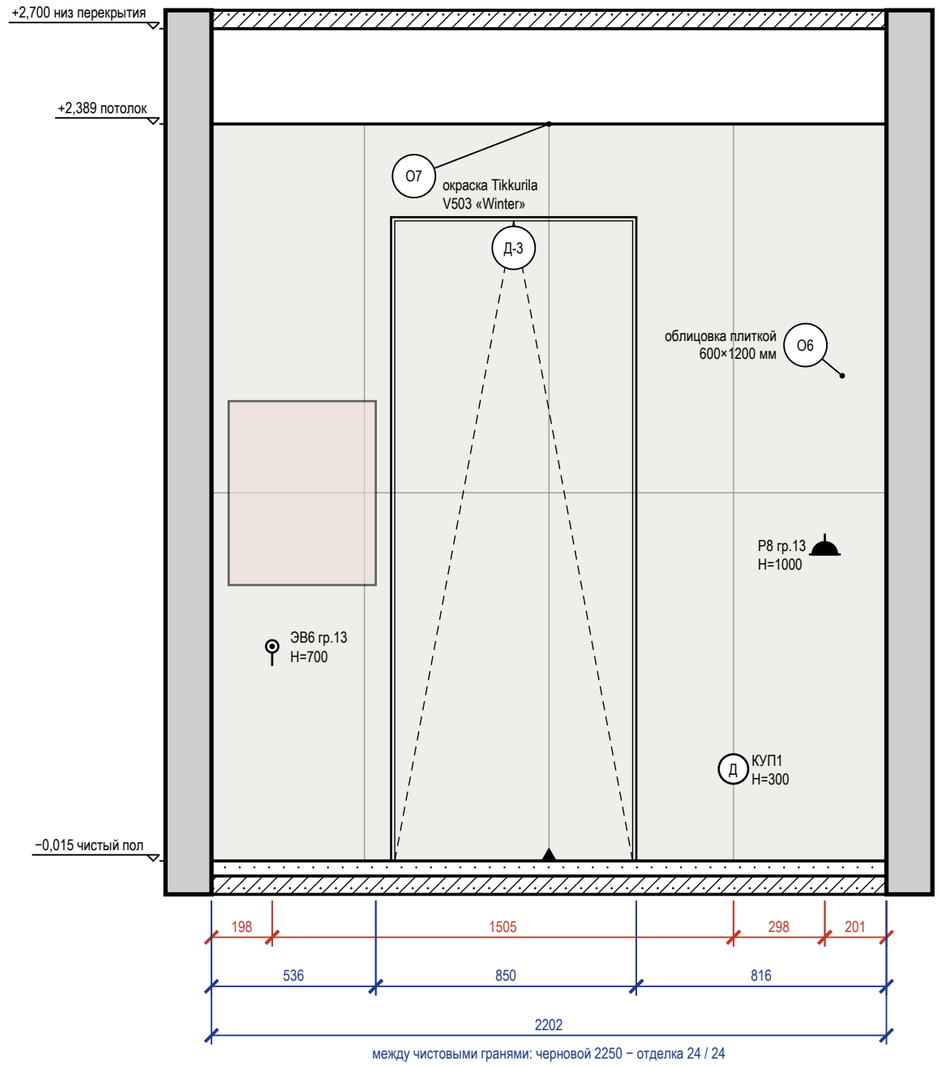


между чистовыми гранями: черновой 2250 − отделка 24 / 24

Развёртка стены Г

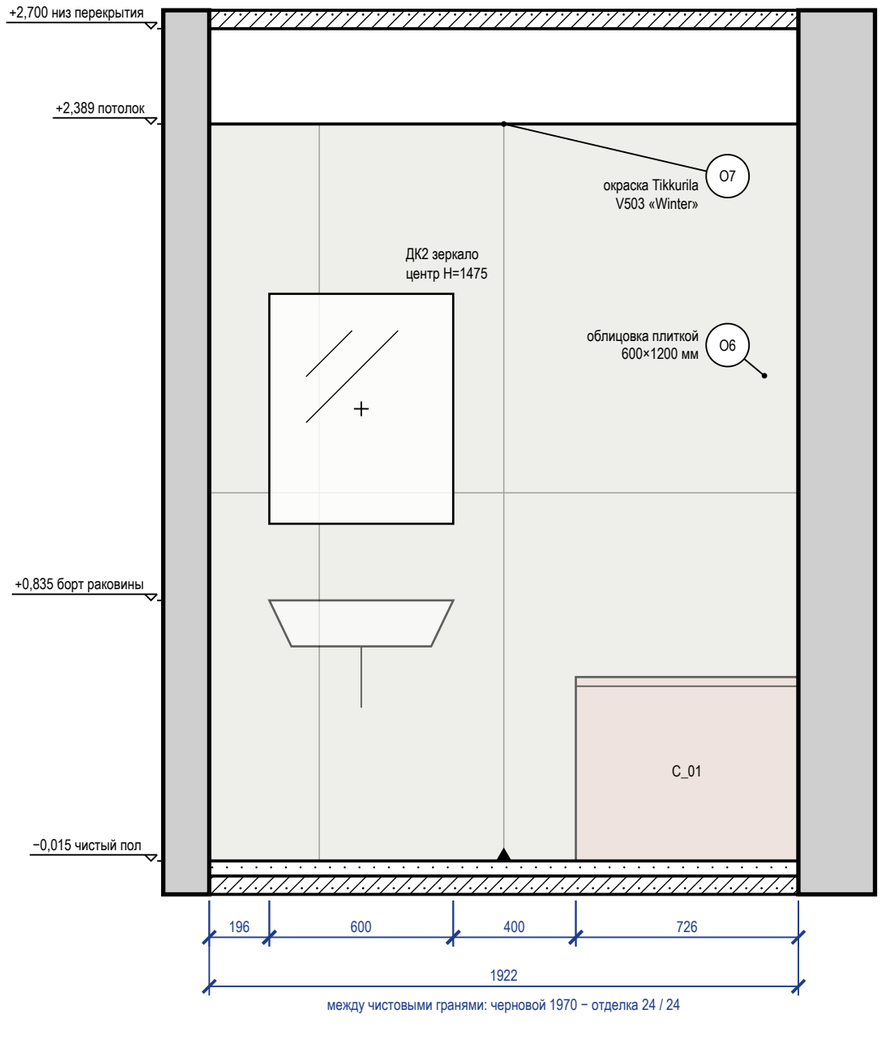

между чистовыми гранями: черновой 1970 − отделка 24 / 24

Схема развёрток (М 1:100)

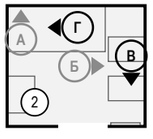

Ведомость отделки (на листе)


Марка	Поверхность	Материал, изделие	Цвет, код	Кол.
О6	стены	облицовка плиткой, 600×1200×9 мм, аналог: керамогранит под травертин, матовый, затирка CG2WA		8,2 м²
О7	потолок	окраска, Tikkurila Luja 7, матовая, подготовка Q3	Tikkurila V503 «Winter»	4,4 м²

Примечания

1. Размеры — в мм от чистовых поверхностей стен; условные обозначения и общие указания — лист 3.
2. Стена Г показана двумя видами: здесь — архитектурная развёртка (мебель, отделка, проёмы, высоты), электроточки и выводы ВК с привязками и таблицей — на листе 52 («Привязки»).
3. Схема мебели, приборов и декора не является технической документацией для производства мебели; габариты — по паспортам изделий.
4. Облицовка — по сетке швов 2 мм, раскладка от оси стены (треугольник у пола), целые ряды от пола; подрезки — по листу раскладки плитки.
5. Гидроизоляция в 2 слоя, заход на стены 200 мм; над ванной — до 2000 и 300 мм за борт — до облицовки, с актом скрытых работ и тестом проливом (узел — на листе узлов).
6. Картины и зеркала крепить к основанию по паспорту изделия (закладные и анкеры — в перечне скрытых работ); крест — ось центра предмета.
7. Двери скрытого монтажа — полотно в плоскости стены, отделка стены по полотну, плинтус прерывается у короба (узел — на листе узлов).

					Проект: Трёхкомнатная квартира	М 1:20
	Лист	№ док.	Подпись	Дата		
Дизайнер	Кырлан А.С.			04.11.26	Развёртки стен В, Г. Ванная (пом. 2)	Стадия: П; Лист: 51; Листов: 92

Развёртка стены Б: электроточки и выводы

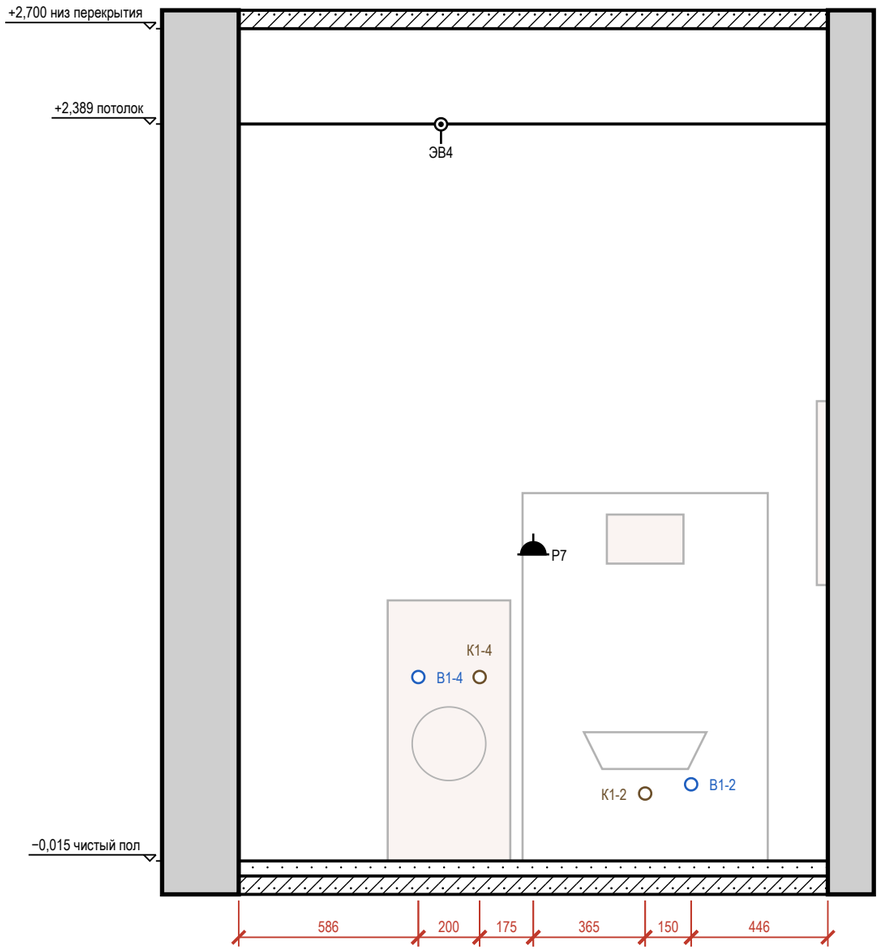

Развёртка стены Г: электроточки и выводы

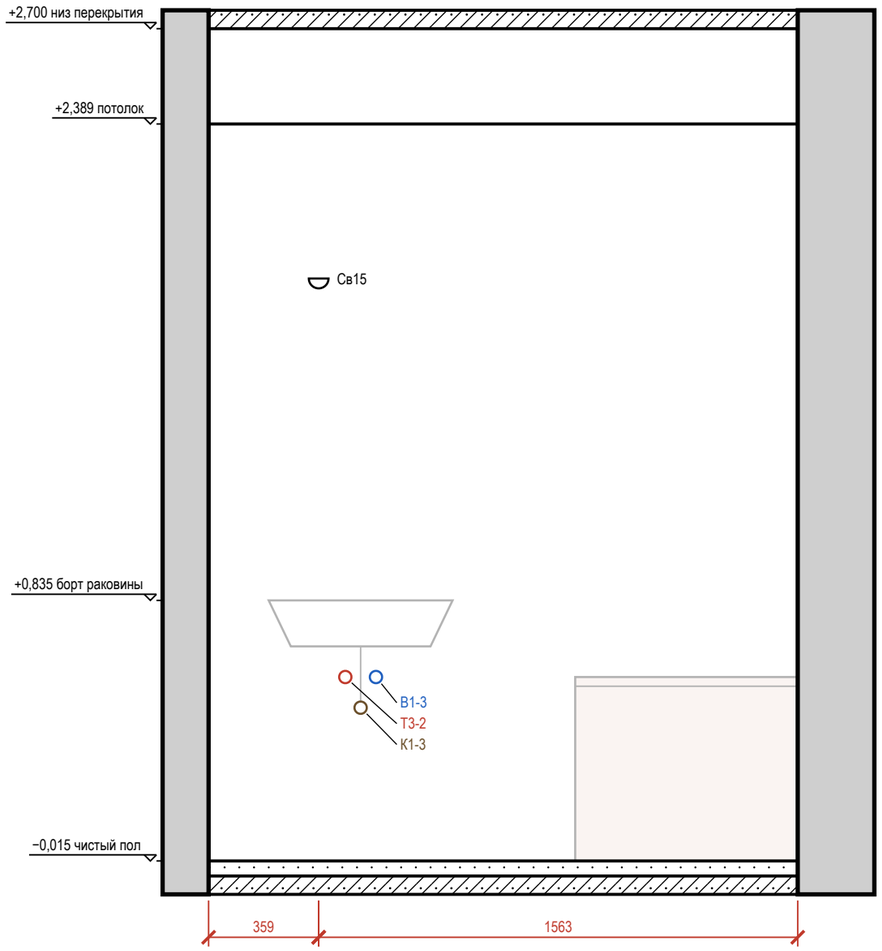


Таблица привязок электроточек и выводов

Стена	Марка	Назначение	От угла, мм	Н от пола, мм	Примечание
Б	В1-4	холодная вода — стиральная машина	586	600	кран машины
Б	ЭВ4	вывод кабеля: вентилятор ВР1 (таймер выбега)	660	2403	гр. 3
Б	К1-4	канализация — стиральная машина	786	600	Ø50
Б	Р7	розетка: стиральная машина	961	1000	гр. 12, IP44
Б	К1-2	канализация — унитаз подвесной	1326	220	Ø110

Стена	Марка	Назначение	От угла, мм	Н от пола, мм	Примечание
Б	В1-2	холодная вода — унитаз подвесной	1476	250	в раме инсталляции
Г	Св15	светильник настенный	359	1900	гр. 3
Г	Т3-2	горячая вода — умывальник	446	600	межос. 100
Г	К1-3	канализация — умывальник	496	500	Ø50
Г	В1-3	холодная вода — умывальник	546	600	межос. 100

Условные обозначения

- розетка влагозащищённая IP44
- вывод кабеля для подключения прибора (без розетки), марка ЭВ
- светильник настенный (бра), Н — высота оси
- вывод В1 (код — в ведомости привязок)
- вывод Т3 (код — в ведомости привязок)
- вывод К1 (код — в ведомости привязок)
- привязки точек и выводов от угла и от пола, мм

Примечания

1. Вид «Привязки» стен Б, Г — электроточки и выводы ВК; архитектурная развёртка (мебель, отделка, проёмы, высоты) — на листах 50, 51. Мебель и приборы подложкой для ориентира; их марки и обозначения мебели, проёмов и стен — там же.
2. Привязки — в мм: по горизонтали от левого чистового угла стены до оси изделия, Н — от чистого пола до оси; все точки — в таблице привязок. Красная цепочка — привязки по осям; точки ближе 120 мм одна к другой в цепочку не дробятся — их привязки только в таблице.
3. У знака — марка электроточки (Р — розетка, S — выключатель, Св — светильник, ЭВ — вывод кабеля); условные обозначения и общие указания — лист 3.
4. Коды выводов ВК: В1 — холодная вода, Т3 — горячая вода, К1 — канализация; номер после дефиса — номер вывода на листе выводов сантехники.


	Лист	№ док.	Подпись	Дата
Дизайнер	Кырлан А.С.			04.11.26

Проект: Трёхкомнатная квартира — **М 1:20**


Привязки электроточек и выводов ВК, стены Б, Г. Ванная (пом. 2)

Стадия	Лист	Листов
П	52	92

Развёртка стены А

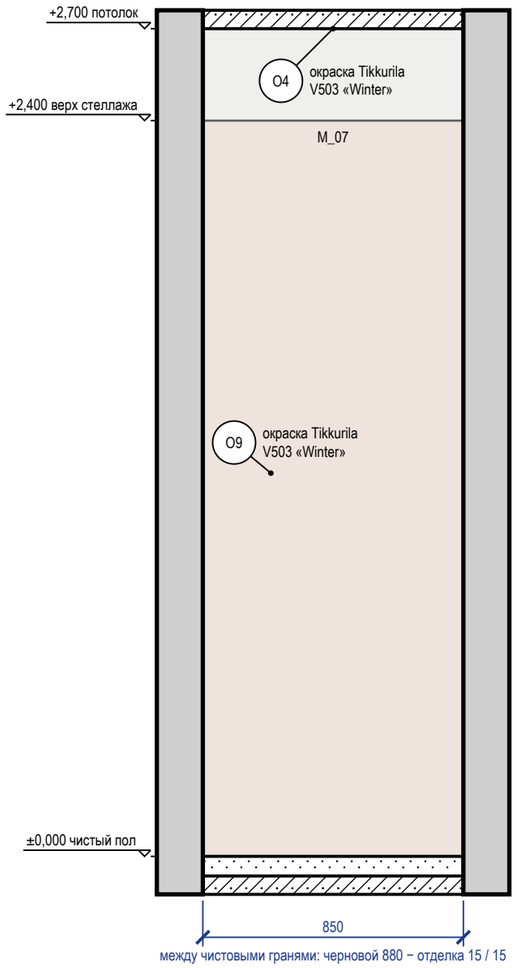

Развёртка стены Б

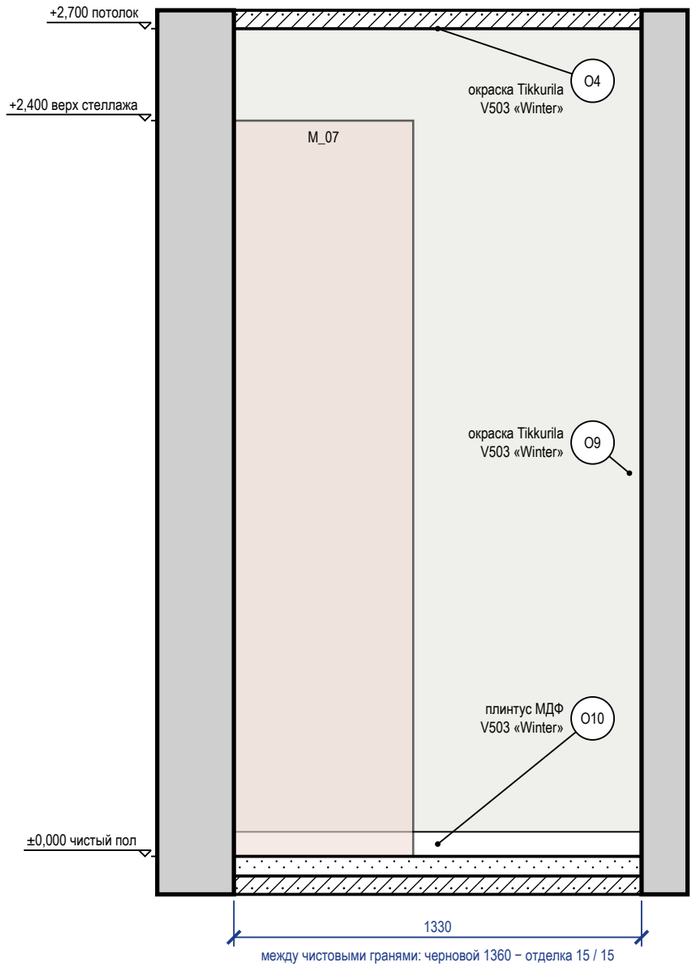

Развёртка стены В


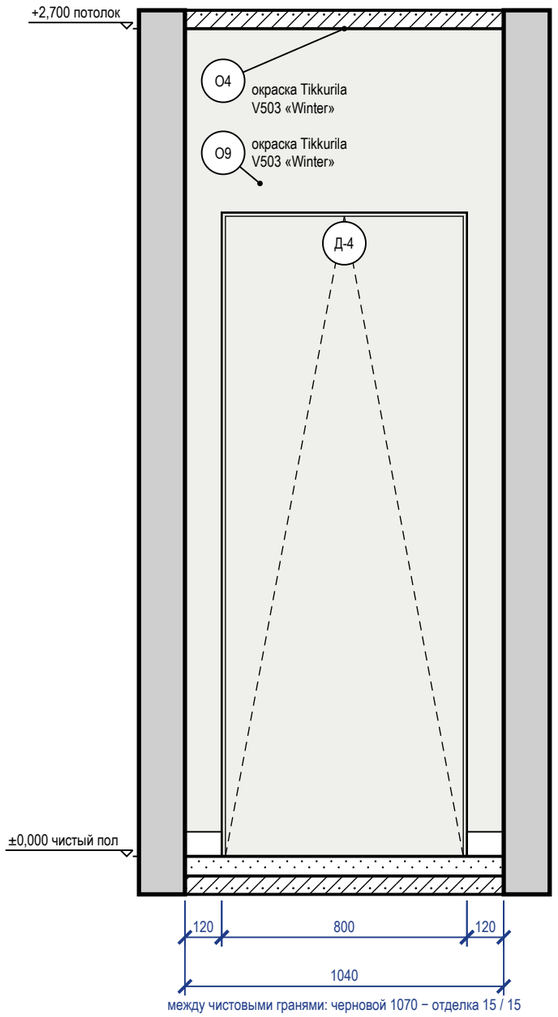


Схема развёрток (М 1:100)

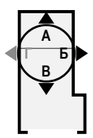

Ведомость отделки (на листе)

Марка	Поверхность	Материал, изделие	Цвет, код	Кол.
O4	потолок	окраска, Tikkurila Anti-Reflex 2, глубокоматовая, подготовка Q3	Tikkurila V503 «Winter»	1,9 м²
O9	стены	окраска, Tikkurila Harmony, матовая, подготовка Q3	Tikkurila V503 «Winter»	7 м²
O10	плинтус	плинтус МДФ, h 80 мм, аналог: плинтус МДФ под покраску 80×16	Tikkurila V503 «Winter»	1,6 м

Примечания

1. Размеры — в мм от чистовых поверхностей стен; условные обозначения и общие указания — лист 3.
2. Двери скрытого монтажа — полотно в плоскости стены, отделка стены по полотну, плинтус прерывается у короба (узел — на листе узлов).

					Проект: Трёхкомнатная квартира	М 1:20
	Лист	№ док.	Подпись	Дата	Развёртки стен А, Б, В. Гардеробная (пом. 3)	Стадия / Лист / Листов
Дизайнер	Кырлан А.С.			04.11.26		П / 53 / 92

Развёртка стены Г


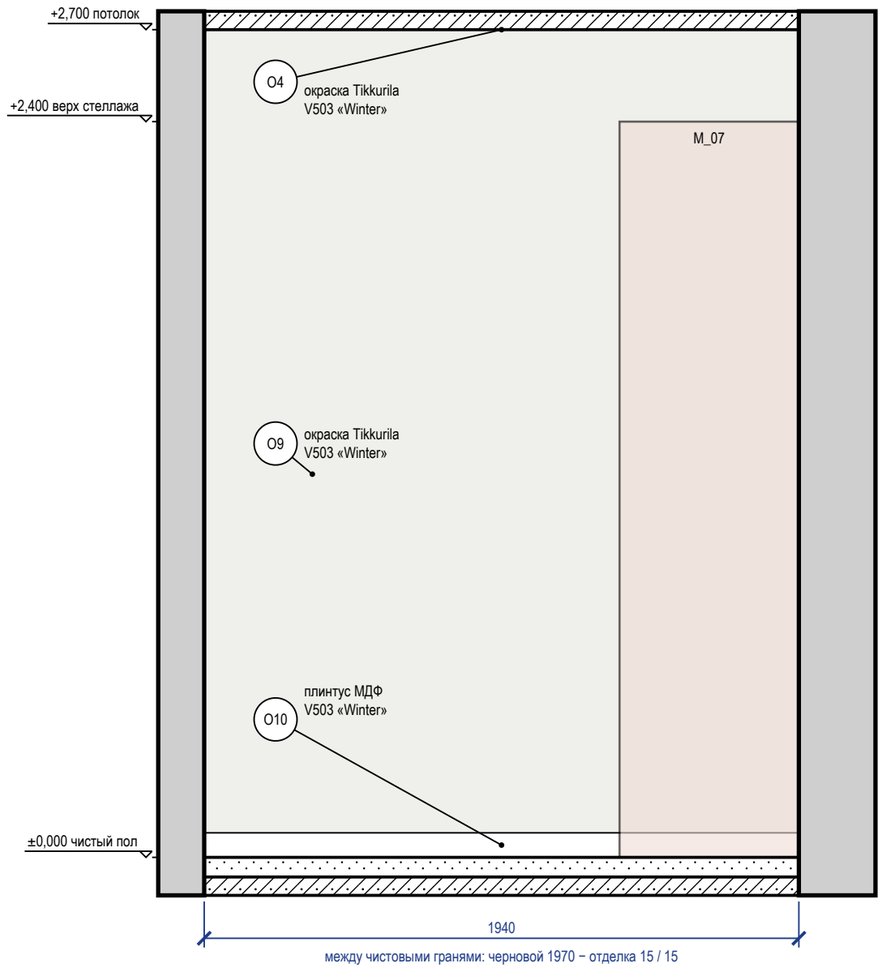


Схема развёрток (М 1:100)

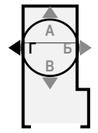

Ведомость отделки (на листе)

Марка	Поверхность	Материал, изделие	Цвет, код	Кол.
O4	потолок	окраска, Tikkurila Anti-Reflex 2, глубокоматовая, подготовка Q3	Tikkurila V503 «Winter»	1,9 м²
O9	стены	окраска, Tikkurila Harmony, матовая, подготовка Q3	Tikkurila V503 «Winter»	5,2 м²
O10	плинтус	плинтус МДФ, h 80 мм, аналог: плинтус МДФ под покраску 80×16	Tikkurila V503 «Winter»	1,9 м

Примечания

1. Размеры — в мм от чистовых поверхностей стен; условные обозначения и общие указания — лист 3.

					Проект: Трёхкомнатная квартира	М 1:20
	Лист	№ док.	Подпись	Дата		
Дизайнер	Кырлан А.С.			04.11.26	Развёртка стены Г. Гардеробная (пом. 3)	
					Стадия: П	Лист: 54 / Листов: 92

Развёртка стены А


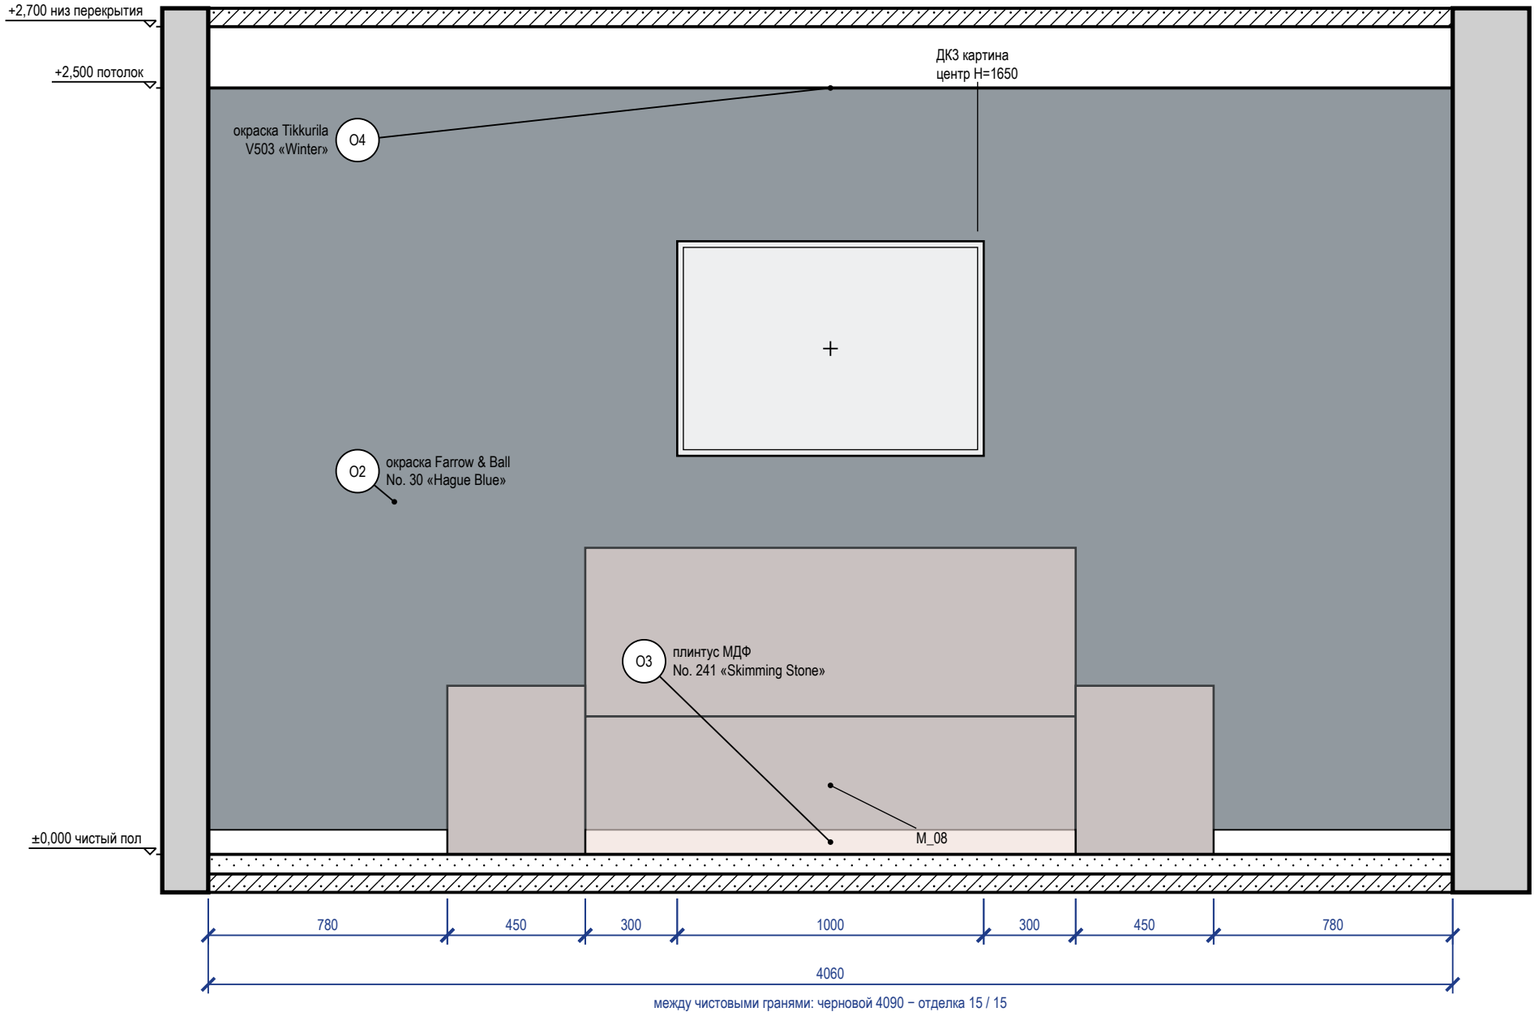


Схема развёрток (М 1:100)

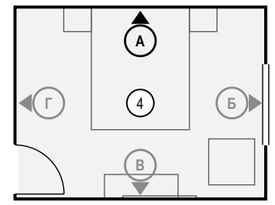

Ведомость отделки (на листе)

Марка	Поверхность	Материал, изделие	Цвет, код	Кол.
O2	акцентная стена	окраска, Farrow & Ball Modern Emulsion, матовая, подготовка Q3	Farrow & Ball No. 30 «Hague Blue»	10,2 м²
O3	плинтус	плинтус МДФ, h 80 мм, аналог: плинтус МДФ под покраску 80×16	Farrow & Ball No. 241 «Skimming Stone»	3,2 м
O4	потолок	окраска, Tikkurila Anti-Reflex 2, глубокоматовая, подготовка Q3	Tikkurila V503 «Winter»	12,8 м²

Примечания

1. Размеры — в мм от чистовых поверхностей стен; условные обозначения и общие указания — лист 3.
2. Стена А показана двумя видами: здесь — архитектурная развёртка (мебель, отделка, проёмы, высоты), электроточки и выводы ВК с привязками и таблицей — на листе 56 («Привязки»).
3. Картины и зеркала крепить к основанию по паспорту изделия (закладные и анкеры — в перечне скрытых работ); крест — ось центра предмета.
4. Потолок — у каждой стены свой, по плану потолков (ПТ1); ступени — зоной, кромка короба перед нишей — тонкой линией; в поле потолка: ПТ2 +2,600.

					Проект: Трёхкомнатная квартира	М 1:20
	Лист	№ док.	Подпись	Дата		
Дизайнер	Кырлан А.С.			04.11.26	Развёртка стены А. Спальня 2 (пом. 4)	
					Стадия: П	Лист: 55
						Листов: 92

Развёртка стены А: электроточки и выводы

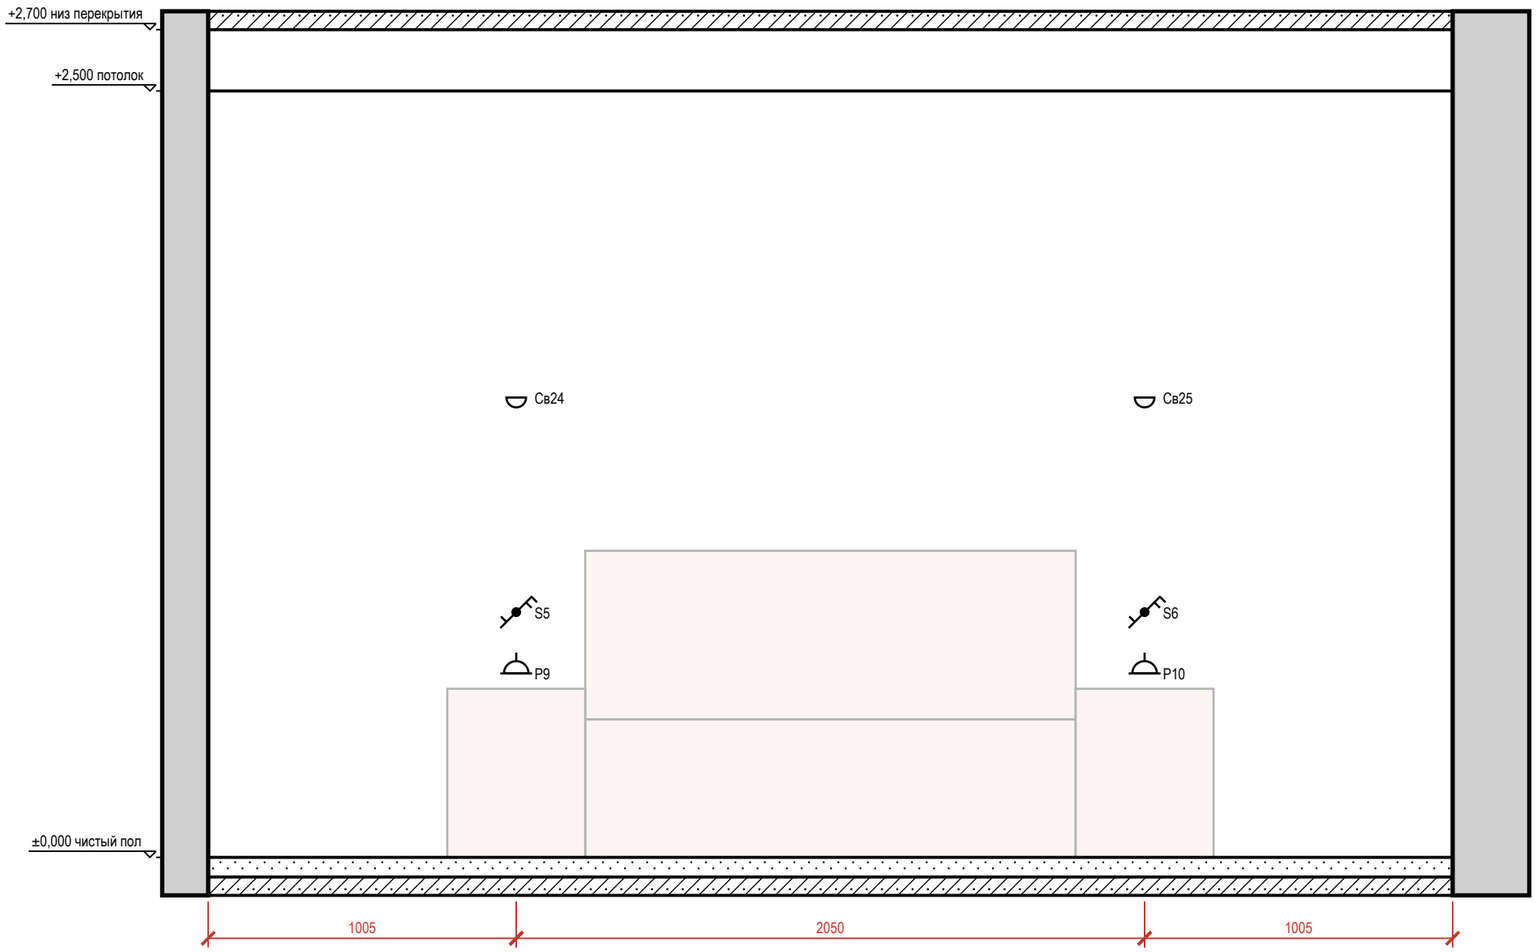



Таблица привязок электроточек и выводов

Марка	Назначение	От угла, мм	Н от пола, мм	Примечание
P9	розетка: у кровати	1005	600	гр. 5
S5	выключатель	1005	800	гр. 1
Св24	светильник настенный	1005	1500	гр. 1
P10	розетка: у кровати	3055	600	гр. 5
S6	выключатель	3055	800	гр. 1
Св25	светильник настенный	3055	1500	гр. 1

Условные обозначения

- розетка с заземляющим контактом; у знака — марка, ×N постов в рамке, гр. — группа щита, Н — высота оси, мм
- выключатель одноклавишный
- выключатель двухклавишный (флажков — по числу клавиш)
- выключатель с проходной или перекрёстной клавишей (обратный флажок); тип клавиши — в подписи
- светильник настенный (бра), Н — высота оси
- привязки точек и выводов от угла и от пола, мм
- А — марка развёртки: буква стены, стрелка — взгляд

Схема развёрток (М 1:100)

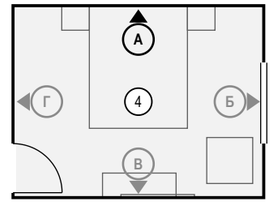

Примечания

1. Вид «Привязки» стены А — электроточки и выводы ВК; архитектурная развёртка (мебель, отделка, проёмы, высоты) — на листе 55. Мебель и приборы — подложкой для ориентира; их марки и обозначения мебели, проёмов и стен — там же.
2. Привязки — в мм: по горизонтали от левого чистового угла стены до оси изделия, Н — от чистого пола до оси; все точки — в таблице привязок. Красная цепочка — привязки по осям; точки ближе 120 мм одна к другой в цепочку не дробятся — их привязки только в таблице.
3. У знака — марка электроточки (Р — розетка, S — выключатель, Св — светильник, ЭВ — вывод кабеля); условные обозначения и общие указания — лист 3.

					Проект: Трёхкомнатная квартира — М 1:20
	Лист	№ док.	Подпись	Дата	
Дизайнер	Кырлан А.С.			04.11.26	Привязки электроточек, стена А. Спальня 2 (пом. 4)

Стадия	Лист	Листов
П	56	92

выпуск 04.11.2026 № 503a52061a · стр. 56 из 92

Развёртка стены Б


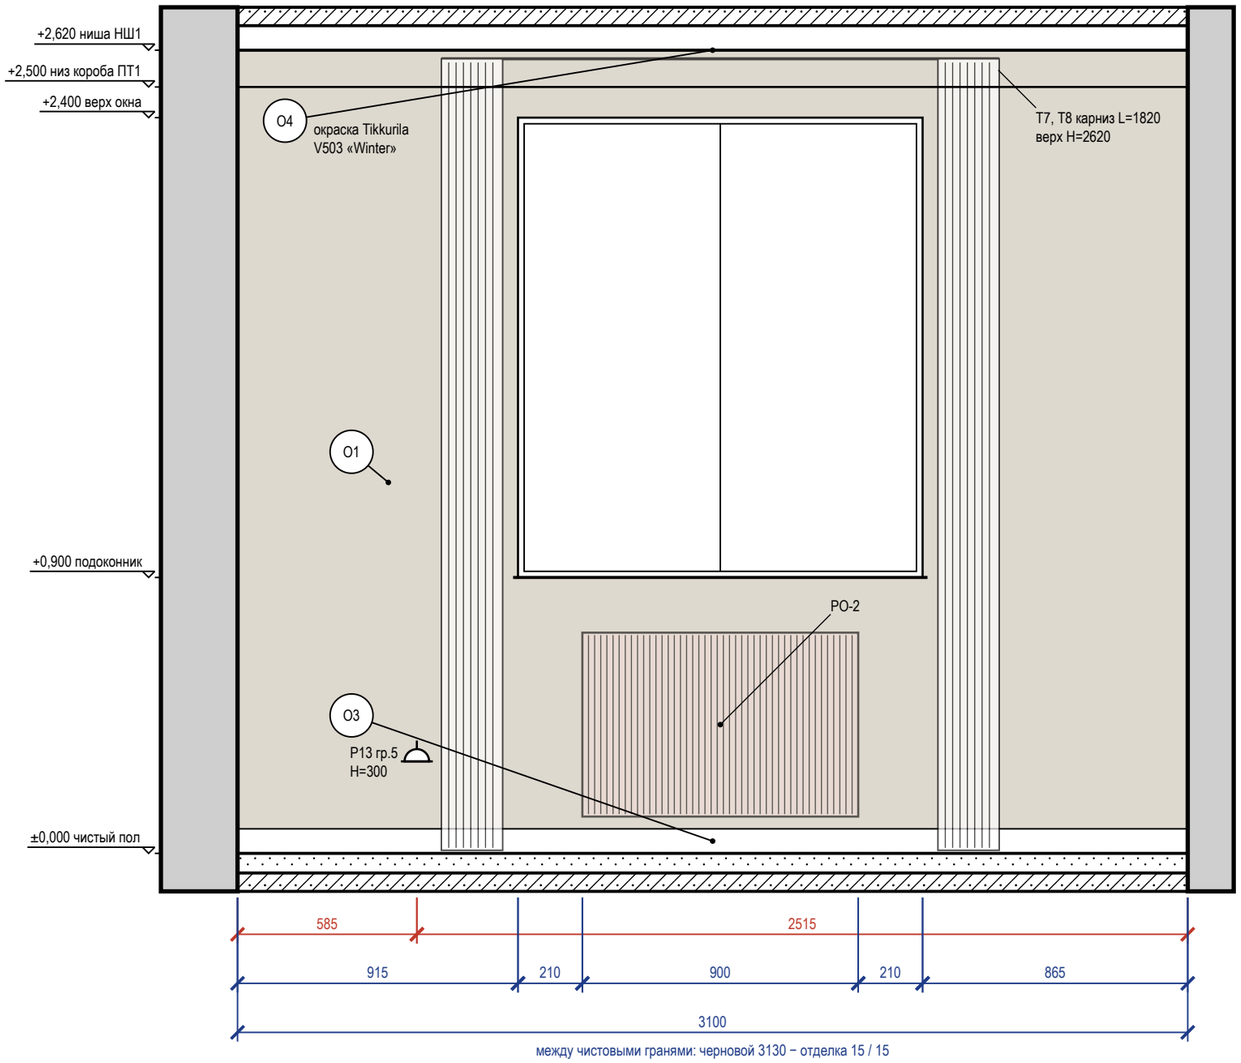


Схема развёрток (М 1:100)

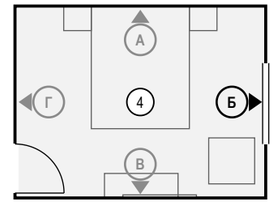

Ведомость отделки (на листе)

Марка	Поверхность	Материал, изделие	Цвет, код	Кол.
О1	стены	окраска, Farrow & Ball Modern Emulsion, матовая, подготовка Q3	Farrow & Ball No. 241 «Skimming Stone»	6,1 м²
О3	плинтус	плинтус МДФ, h 80 мм, аналог: плинтус МДФ под покраску 80×16	Farrow & Ball No. 241 «Skimming Stone»	3,1 м
О4	потолок	окраска, Tikkurila Anti-Reflex 2, глубокоматовая, подготовка Q3	Tikkurila V503 «Winter»	12,8 м²

Примечания

1. Размеры — в мм от чистовых поверхностей стен; условные обозначения и общие указания — лист 3.
2. Карнизы (шины) — по ведомости текстиля декоратора: длина L и верх H на развёртке — те же числа, что в ведомости; крепление — до окраски потолка.
3. Потолок — у каждой стены свой, по плану потолков (НШ1, ПТ1); ступени — зоной, кромка короба перед нишей — тонкой линией; в поле потолка: ПТ2 +2,600.

					Проект: Трёхкомнатная квартира	М 1:20
	Лист	№ док.	Подпись	Дата	Развёртка стены Б. Спальня 2 (пом. 4)	Стадия / Лист / Листов
Дизайнер	Кырлан А.С.			04.11.26		П / 57 / 92

Развёртка стены В


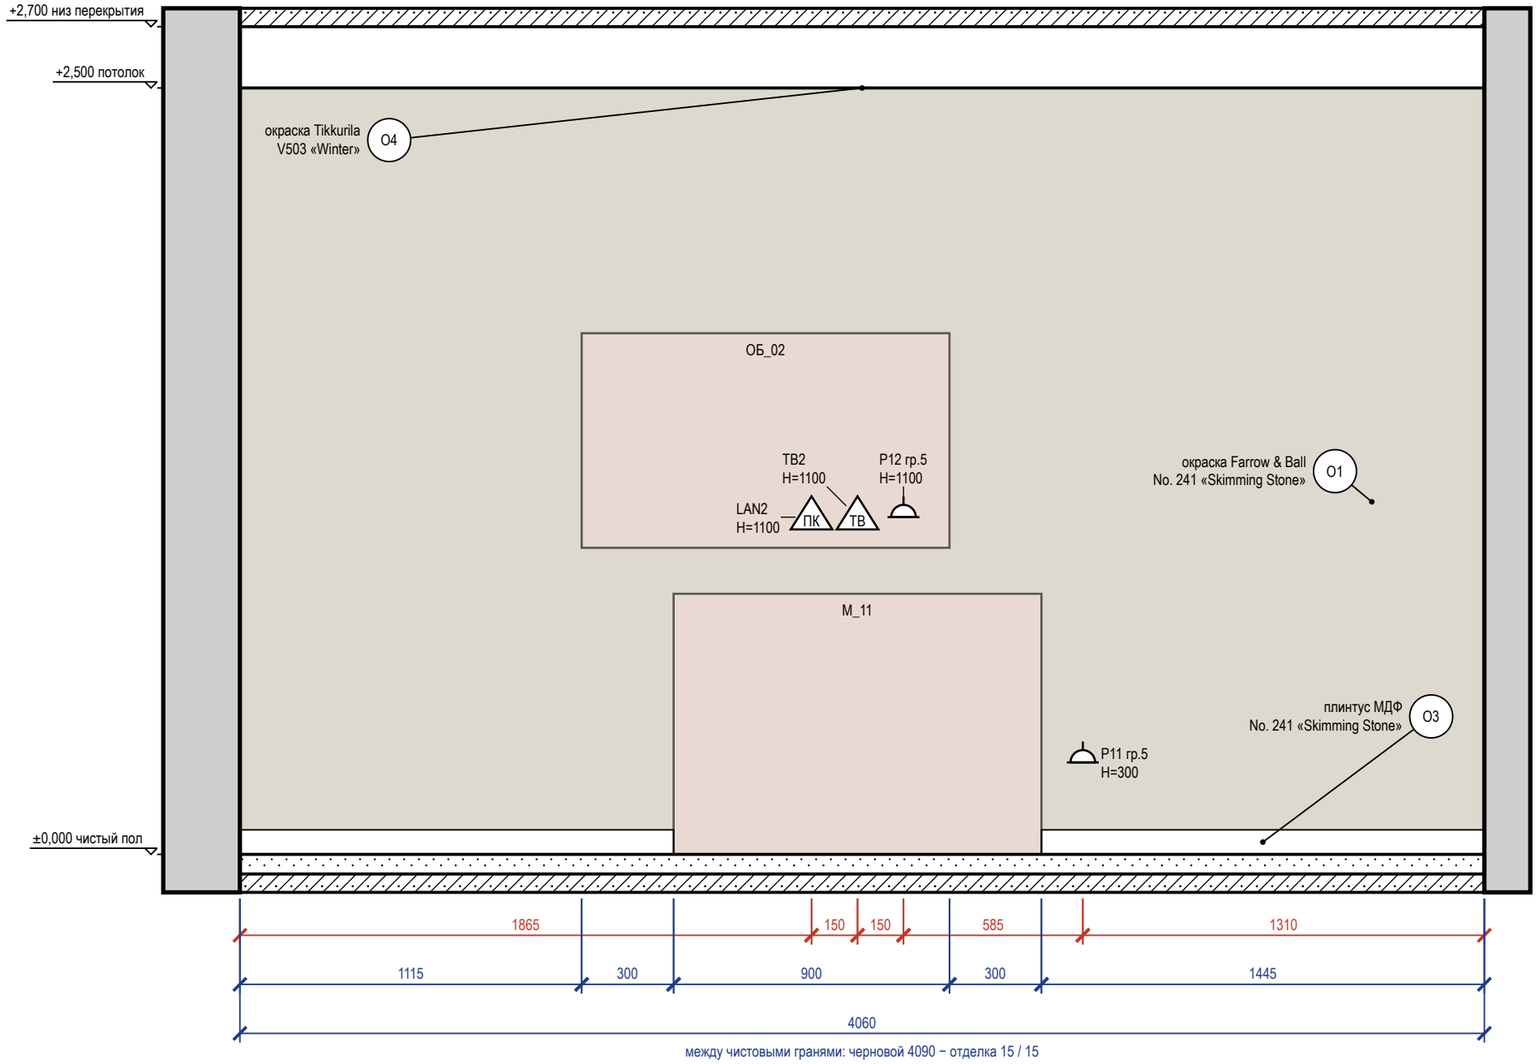


Схема развёрток (М 1:100)

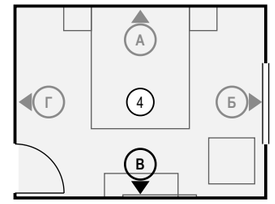

Ведомость отделки (на листе)

Марка	Поверхность	Материал, изделие	Цвет, код	Кол.
О1	стены	окраска, Farrow & Ball Modern Emulsion, матовая, подготовка Q3	Farrow & Ball No. 241 «Skimming Stone»	10,2 м²
О3	плинтус	плинтус МДФ, h 80 мм, аналог: плинтус МДФ под покраску 80×16	Farrow & Ball No. 241 «Skimming Stone»	2,9 м
О4	потолок	окраска, Tikkurila Anti-Reflex 2, глубокоматовая, подготовка Q3	Tikkurila V503 «Winter»	12,8 м²

Примечания

1. Размеры — в мм от чистовых поверхностей стен; условные обозначения и общие указания — лист 3.
2. Потолок — у каждой стены свой, по плану потолков (ПТ1); ступени — зоной, кромка короба перед нишей — тонкой линией; в поле потолка: ПТ2 +2,600.

					Проект: Трёхкомнатная квартира — М 1:20
	Лист	№ док.	Подпись	Дата	Развёртка стены В. Спальня 2 (пом. 4)
Дизайнер	Кырлан А.С.			04.11.26	

Стадия	Лист	Листов
П	58	92

Развёртка стены Г


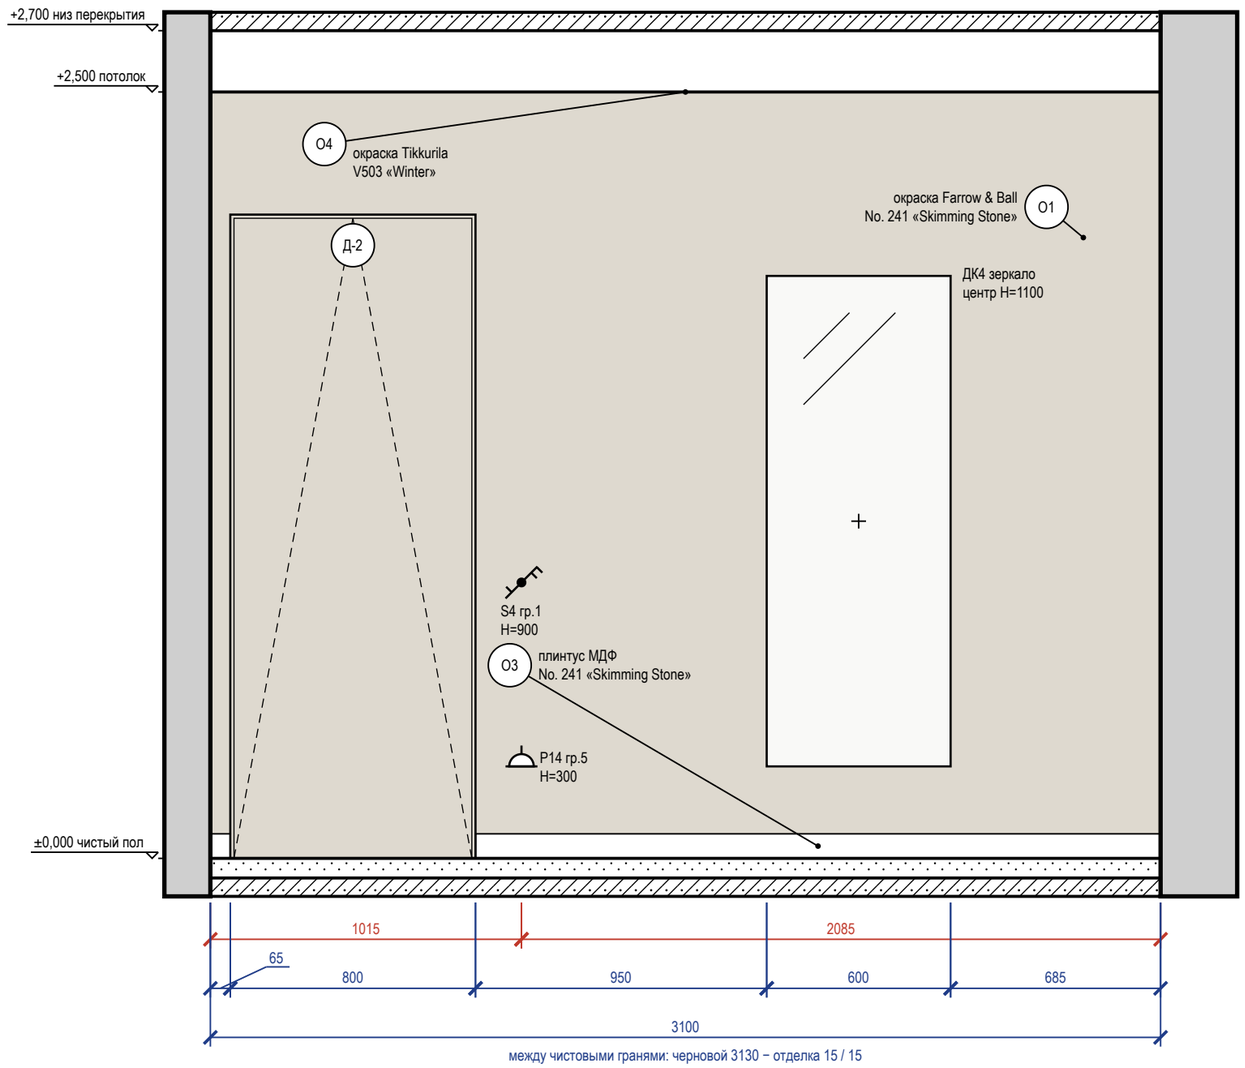


Схема развёрток (М 1:100)

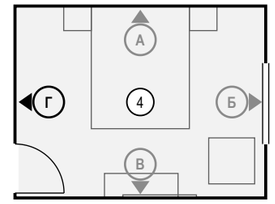

Ведомость отделки (на листе)


Марка	Поверхность	Материал, изделие	Цвет, код	Кол.
О1	стены	окраска, Farrow & Ball Modern Emulsion, матовая, подготовка Q3	Farrow & Ball No. 241 «Skimming Stone»	6,1 м²
О3	плинтус	плинтус МДФ, h 80 мм, аналог: плинтус МДФ под покраску 80×16	Farrow & Ball No. 241 «Skimming Stone»	2,3 м
О4	потолок	окраска, Tikkurila Anti-Reflex 2, глубокоматовая, подготовка Q3	Tikkurila V503 «Winter»	12,8 м²

Примечания

1. Размеры — в мм от чистовых поверхностей стен; условные обозначения и общие указания — лист 3.
2. Картины и зеркала крепить к основанию по паспорту изделия (закладные и анкеры — в перечне скрытых работ); крест — ось центра предмета.
3. Двери скрытого монтажа — полотно в плоскости стены, отделка стены по полотну, плинтус прерывается у короба (узел — на листе узлов).
4. Потолок — у каждой стены свой, по плану потолков (ПТ1); ступени — зоной, кромка короба перед нишей — тонкой линией; в поле потолка: ПТ2 +2,600.


					Проект: Трёхкомнатная квартира — М 1:20
	Лист	№ док.	Подпись	Дата	
Дизайнер	Кырлан А.С.			04.11.26	Развёртка стены Г. Спальня 2 (пом. 4)
					Стадия: П; Лист: 59; Листов: 92

Развёртка стены А

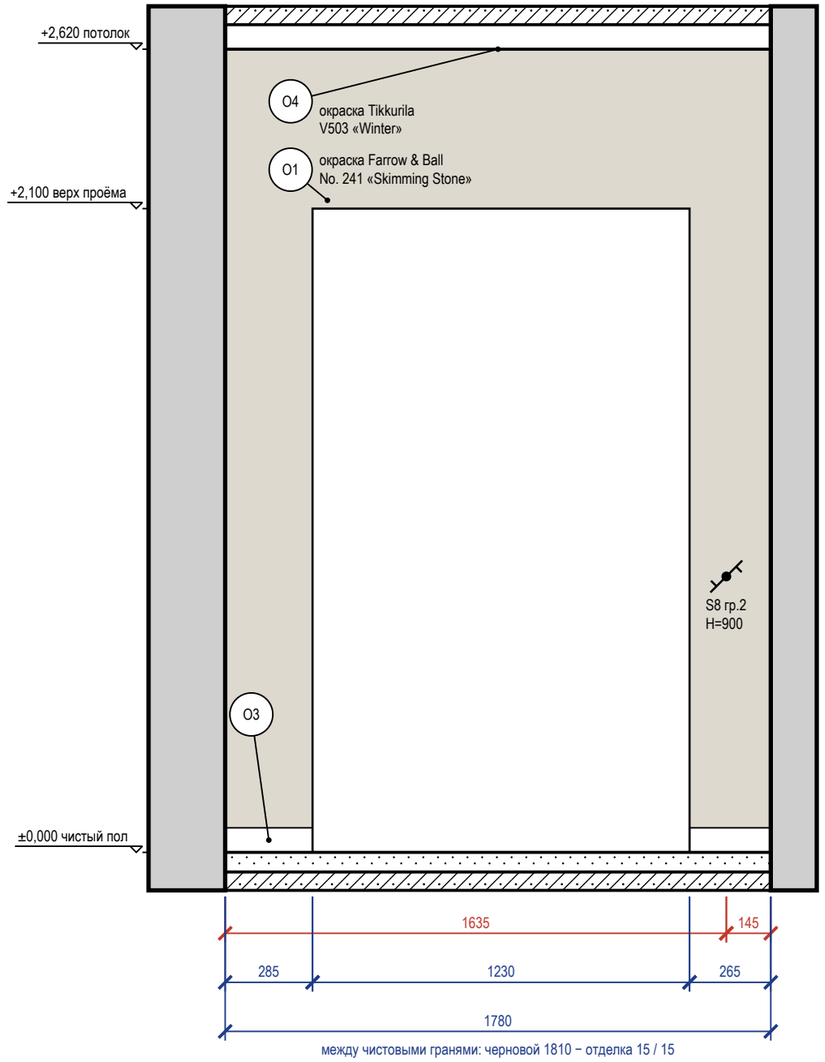


между чистовыми гранями: черновой 1810 − отделка 15 / 15

Развёртка стены В

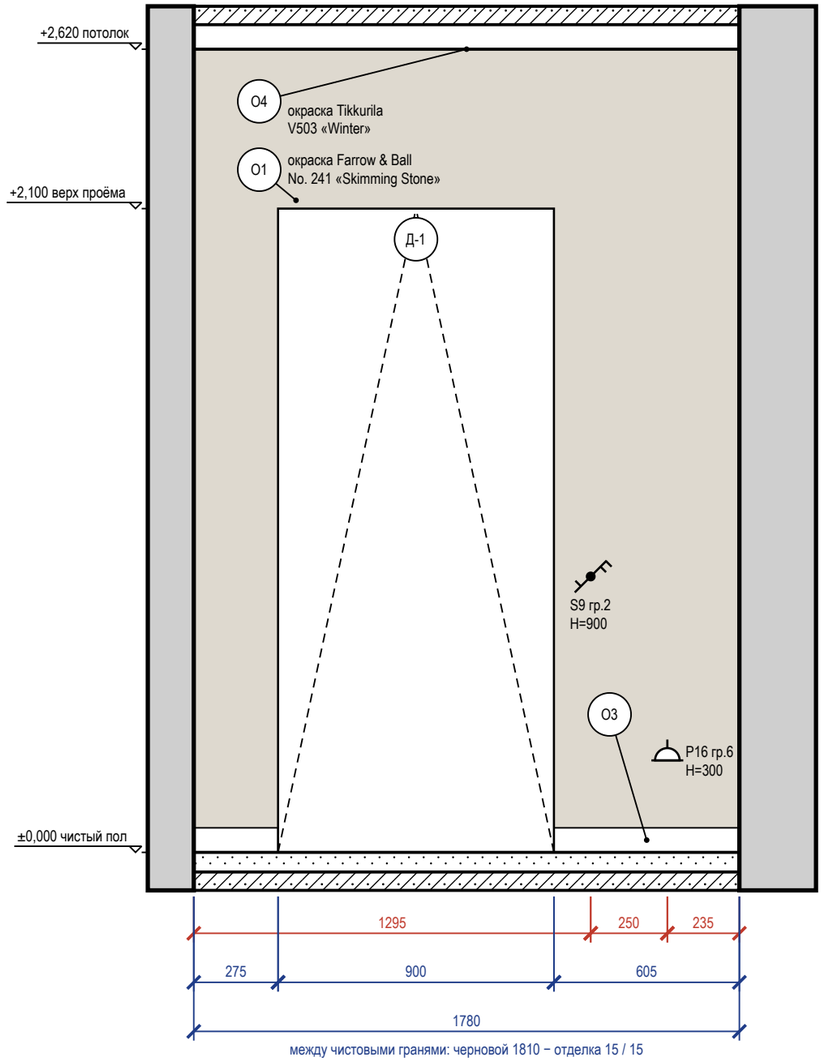

между чистовыми гранями: черновой 1810 − отделка 15 / 15

Схема развёрток (М 1:100)

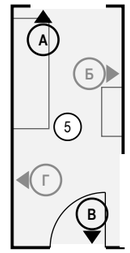

Ведомость отделки (на листе)

Марка	Поверхность	Материал, изделие	Цвет, код	Кол.
О1	стены	окраска, Farrow & Ball Modern Emulsion, матовая, подготовка Q3	Farrow & Ball No. 241 «Skimming Stone»	4,9 м²
О3	плинтус	плинтус МДФ, h 80 мм, аналог: плинтус МДФ под покраску 80×16	Farrow & Ball No. 241 «Skimming Stone»	1,4 м
О4	потолок	окраска, Tikkurila Anti-Reflex 2, глубокоматовая, подготовка Q3	Tikkurila V503 «Winter»	7,1 м²

Примечания

1. Размеры — в мм от чистовых поверхностей стен; условные обозначения и общие указания — лист 3.

	Лист	№ док.	Подпись	Дата
Дизайнер	Кырлан А.С.			04.11.26

Проект: Трёхкомнатная квартира — М 1:20

Развёртки стен А, В. Прихожая (пом. 5)

Стадия	Лист	Листов
П	60	92

выпуск 04.11.2026 № 503a52061a · стр. 60 из 92

Развёртка стены Б


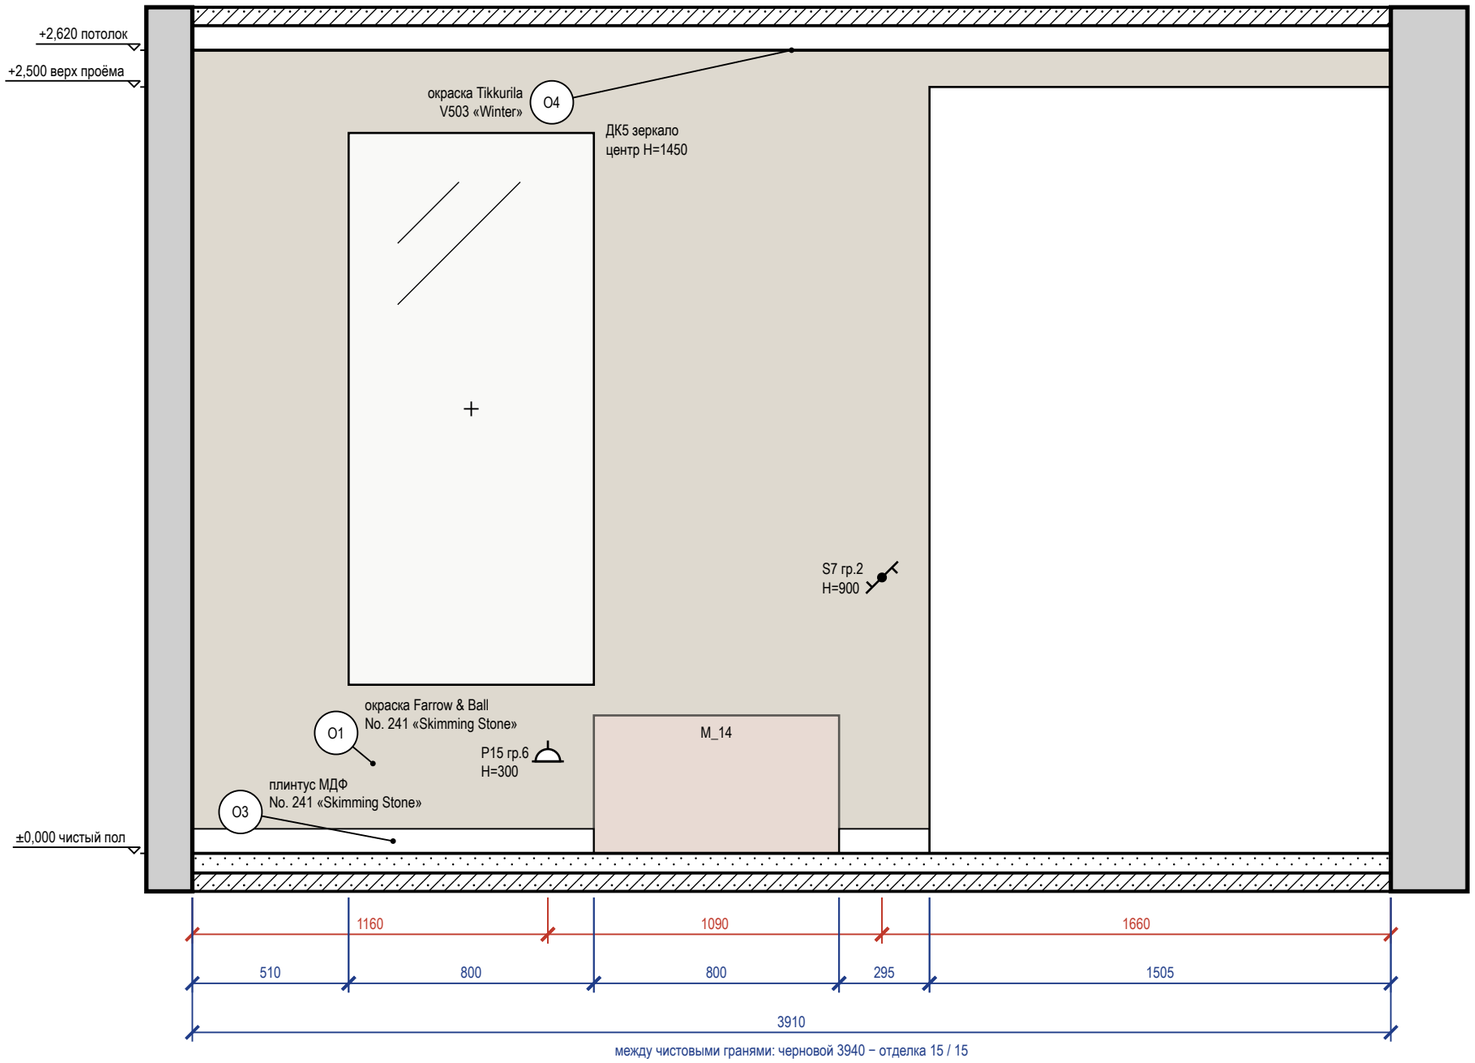


Схема развёрток (М 1:100)

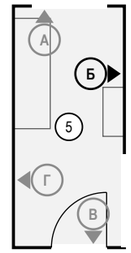

Ведомость отделки (на листе)

Марка	Поверхность	Материал, изделие	Цвет, код	Кол.
О1	стены	окраска, Farrow & Ball Modern Emulsion, матовая, подготовка Q3	Farrow & Ball No. 241 «Skimming Stone»	6,5 м²
О3	плинтус	плинтус МДФ, h 80 мм, аналог: плинтус МДФ под покраску 80×16	Farrow & Ball No. 241 «Skimming Stone»	1,6 м
О4	потолок	окраска, Tikkurila Anti-Reflex 2, глубокоматовая, подготовка Q3	Tikkurila V503 «Winter»	7,1 м²

Примечания

1. Размеры — в мм от чистовых поверхностей стен; условные обозначения и общие указания — лист 3.
2. Картины и зеркала крепить к основанию по паспорту изделия (закладные и анкеры — в перечне скрытых работ); крест — ось центра предмета.

	Лист	№ док.	Подпись	Дата
Дизайнер	Кырлан А.С.			04.11.26

Проект: Трёхкомнатная квартира — **М 1:20**

Развёртка стены Б. Прихожая (пом. 5)

Стадия	Лист	Листов
П	61	92

Развёртка стены Г


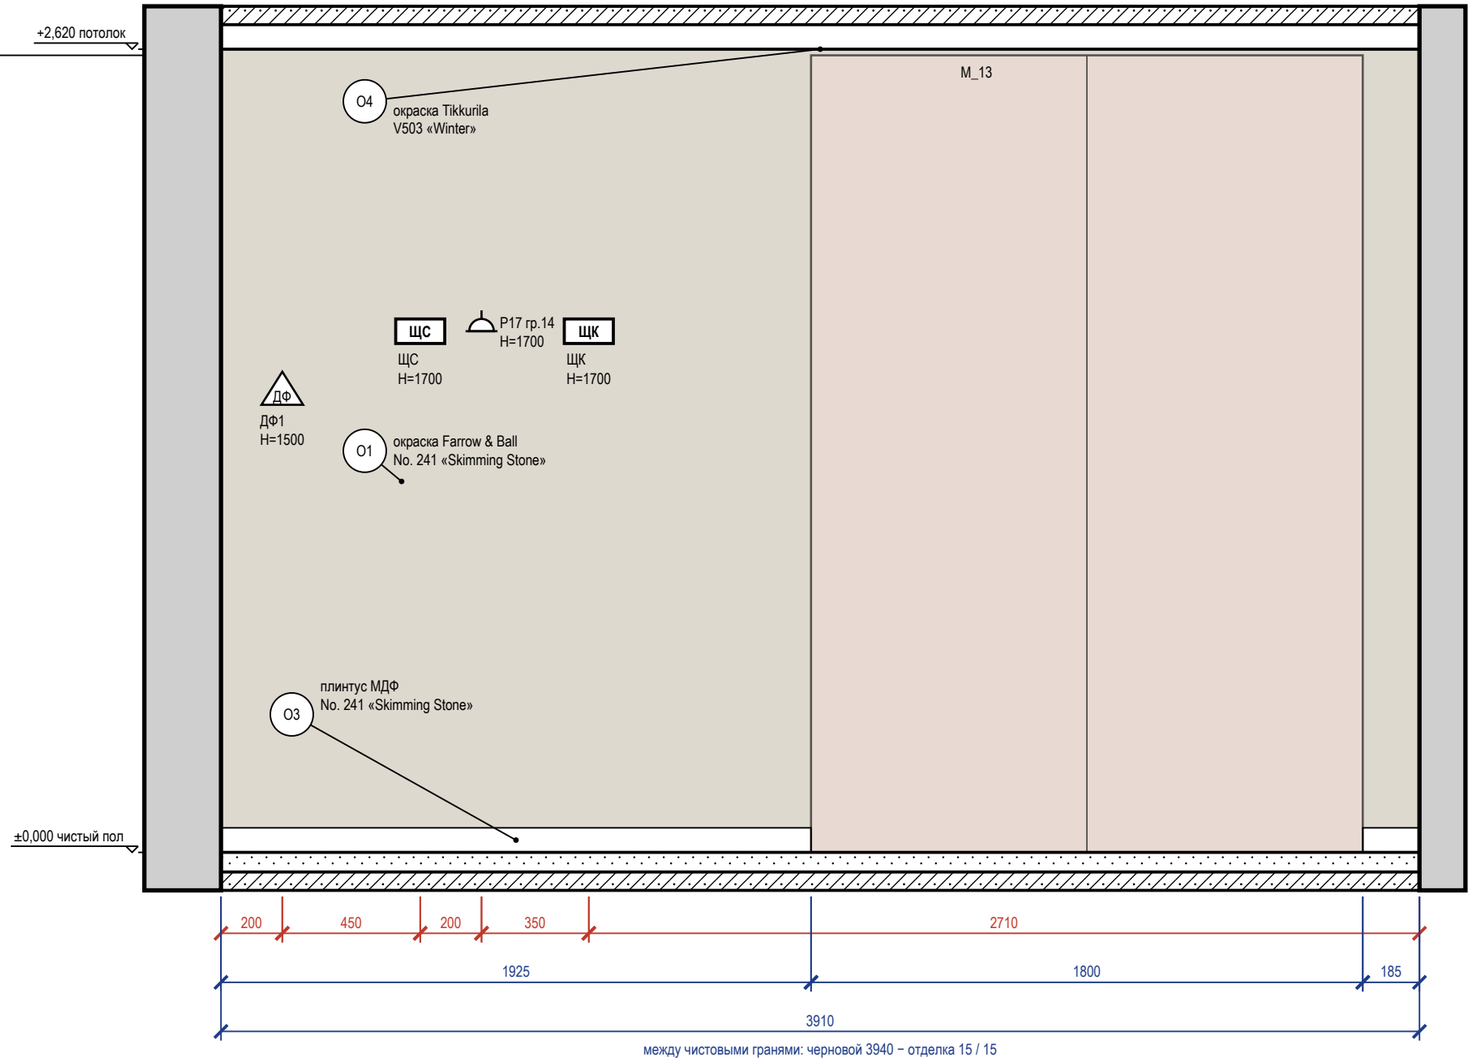


Схема развёрток (М 1:100)

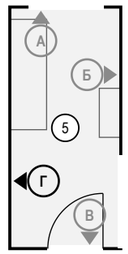

Ведомость отделки (на листе)

Марка	Поверхность	Материал, изделие	Цвет, код	Кол.
О1	стены	окраска, Farrow & Ball Modern Emulsion, матовая, подготовка Q3	Farrow & Ball No. 241 «Skimming Stone»	10,2 м²
О3	плинтус	плинтус МДФ, h 80 мм, аналог: плинтус МДФ под покраску 80×16	Farrow & Ball No. 241 «Skimming Stone»	2,1 м
О4	потолок	окраска, Tikkurila Anti-Reflex 2, глубокоматовая, подготовка Q3	Tikkurila V503 «Winter»	7,1 м²

Примечания

1. Размеры — в мм от чистовых поверхностей стен; условные обозначения и общие указания — лист 3.

					Проект: Трёхкомнатная квартира	М 1:20
	Лист	№ док.	Подпись	Дата		
Дизайнер	Кырлан А.С.			04.11.26	Развёртка стены Г. Прихожая (пом. 5)	Стадия: П; Лист: 62; Листов: 92

Развёртка стены Б2


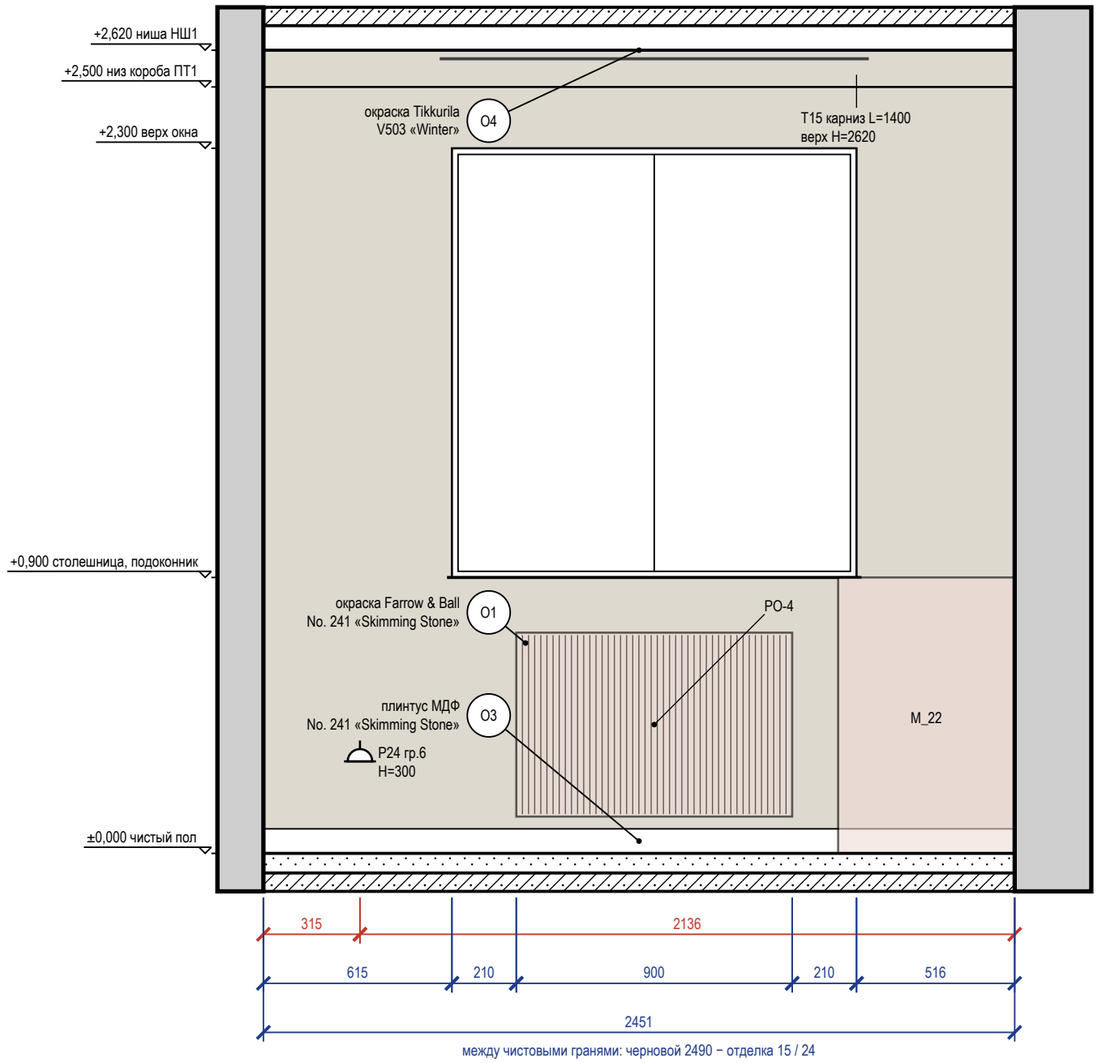


Схема развёрток (М 1:100)

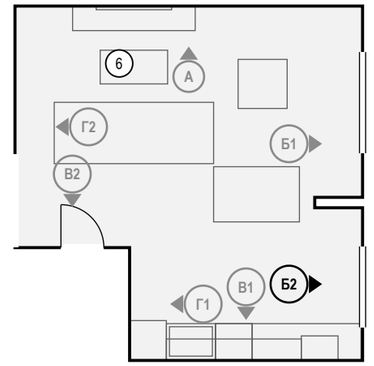

Ведомость отделки (на листе)

Марка	Поверхность	Материал, изделие	Цвет, код	Кол.
O1	стены	окраска, Farrow & Ball Modern Emulsion, матовая, подготовка Q3	Farrow & Ball No. 241 «Skimming Stone»	4,6 м²
O3	плинтус	плинтус МДФ, h 80 мм, аналог: плинтус МДФ под покраску 80×16	Farrow & Ball No. 241 «Skimming Stone»	2,5 м
O4	потолок	окраска, Tikkurila Anti-Reflex 2, глубокоматовая, подготовка Q3	Tikkurila V503 «Winter»	29,2 м²

Примечания

1. Размеры — в мм от чистовых поверхностей стен; условные обозначения и общие указания — лист 3.
2. Карнизы (шины) — по ведомости текстиля декоратора: длина L и верх H на развёртке — те же числа, что в ведомости; крепление — до окраски потолка.
3. Выводы кухонной техники — по утверждённому проекту кухни: привязки выводов даются от осей модулей гарнитура.
4. Потолок — у каждой стены свой, по плану потолков (НШ1, ПТ1); ступени — зоной, кромка короба перед нишей — тонкой линией; в поле потолка: ПТ2 +2,600.

					Проект: Трёхкомнатная квартира	М 1:20
	Лист	№ док.	Подпись	Дата	Развёртка стены Б2. Кухня-гостиная (пом. 6), кухонный фронт	Стадия / Лист / Листов
Дизайнер	Кырлан А.С.			04.11.26		П / 63 / 92

Развёртка стены В1


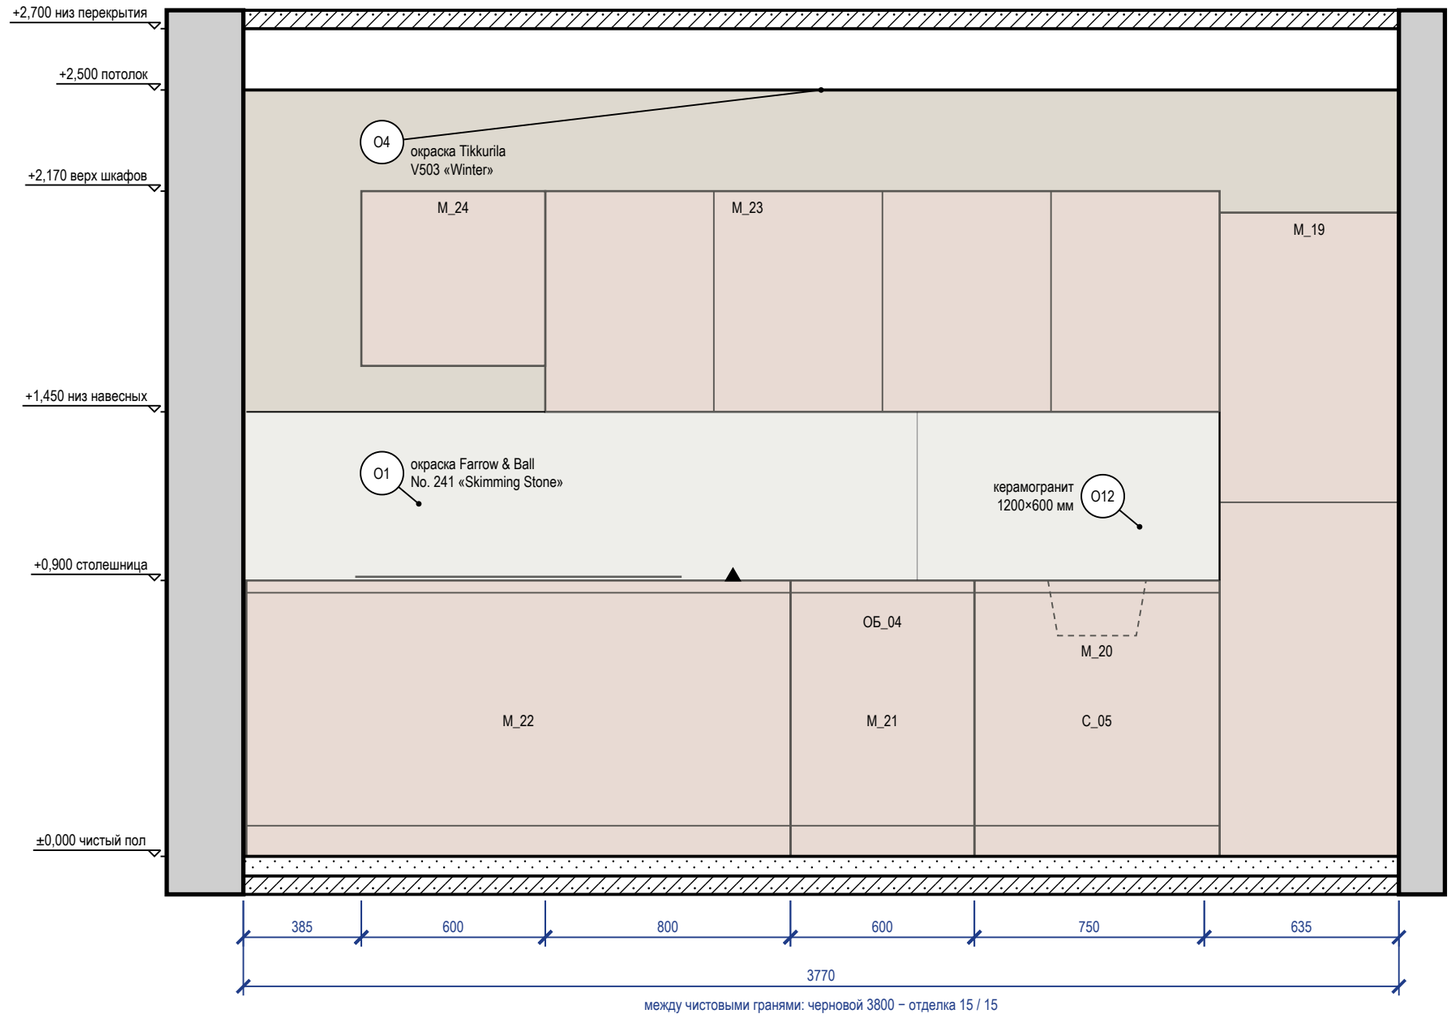


Схема развёрток (М 1:100)

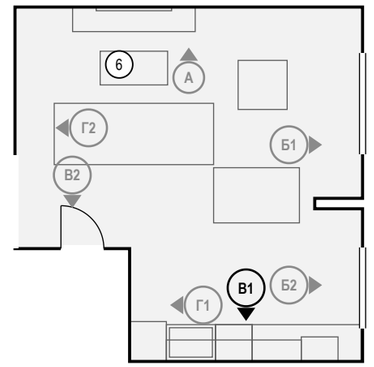

Ведомость отделки (на листе)

Марка	Поверхность	Материал, изделие	Цвет, код	Кол.
О1	стены	окраска, Farrow & Ball Modern Emulsion, матовая, подготовка Q3	Farrow & Ball No. 241 «Skimming Stone»	7,7 м²
О4	потолок	окраска, Tikkurila Anti-Reflex 2, глубокоматовая, подготовка Q3	Tikkurila V503 «Winter»	29,2 м²
О12	фартук	керамогранит, 1200×600×9 мм, аналог: керамогранит под травертин, матовый, затирка CG2WA		1,7 м²

Примечания

1. Размеры — в мм от чистовых поверхностей стен; условные обозначения и общие указания — лист 3.
2. Стена В1 показана двумя видами: здесь — архитектурная развёртка (мебель, отделка, проёмы, высоты), электроточки и выводы ВК с привязками и таблицей — на листе 65 («Привязки»).
3. Схема мебели, приборов и декора не является технической документацией для производства мебели; габариты — по паспортам изделий.
4. Потолок — у каждой стены свой, по плану потолков (ПТ1); ступени — зоной, кромка короба перед нишей — тонкой линией; в поле потолка: ПТ2 +2,600.

					Проект: Трёхкомнатная квартира	М 1:20
	Лист	№ док.	Подпись	Дата	Развёртка стены В1. Кухня-гостиная (пом. 6), кухонный фронт	
Дизайнер	Кырлан А.С.			04.11.26		

Стадия	Лист	Листов
П	64	92

Развёртка стены В1: электроточки и выводы

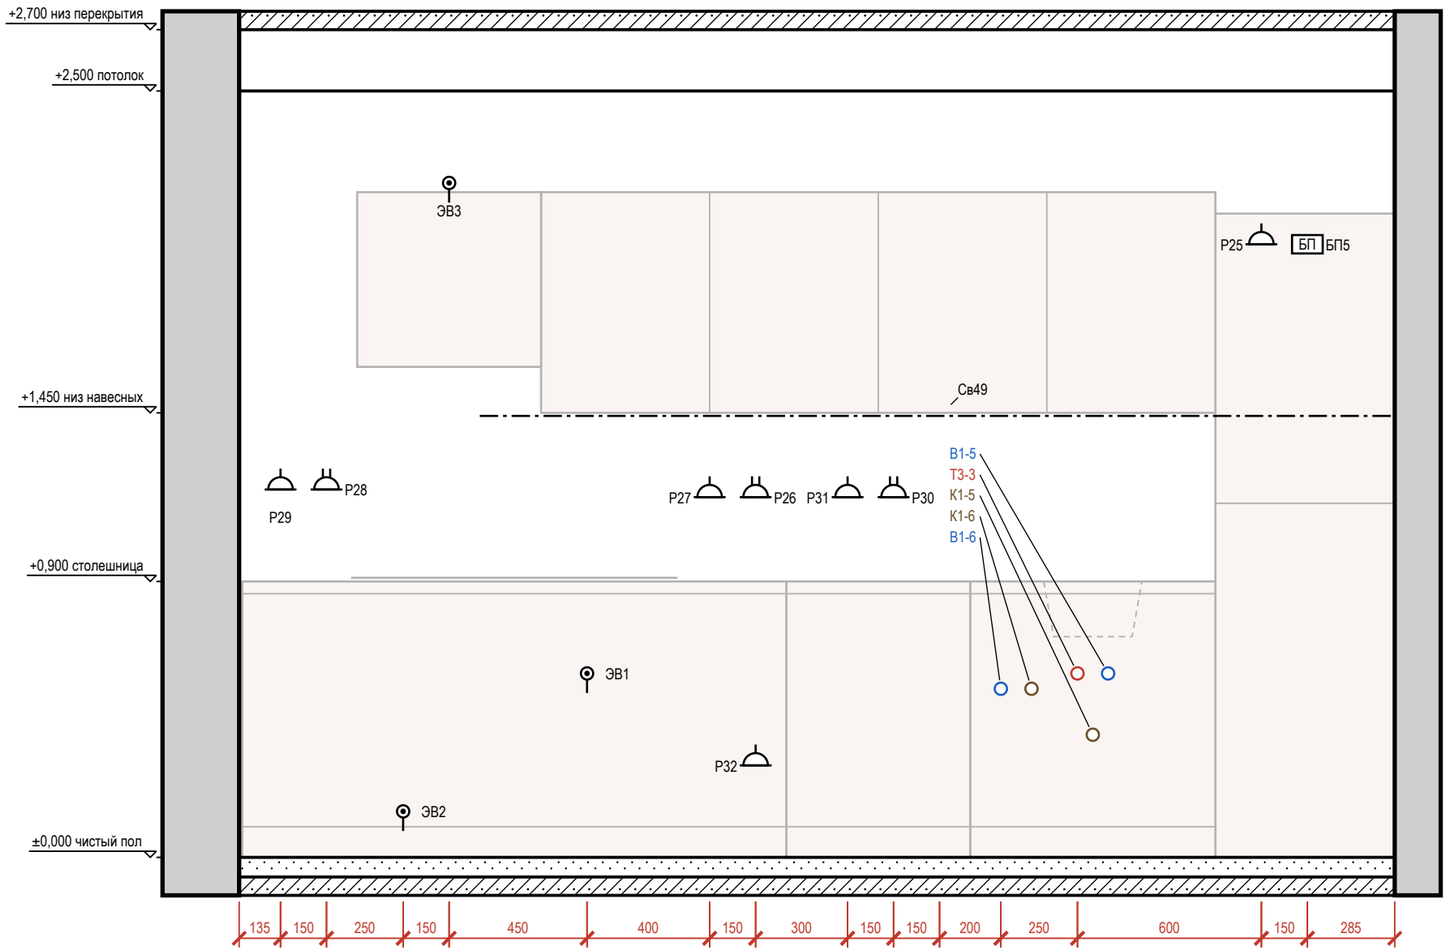


Таблица привязок электроточек и выводов

Марка	Назначение	От угла, мм	Н от пола, мм	Примечание
Р29	розетка: фартук	135	1200	гр. 7
Р28	розетка: фартук	285	1200	рамка 2 поста, гр. 7
ЭВ2	вывод кабеля: духовой шкаф	535	150	гр. 9
ЭВ3	вывод кабеля: вытяжка — над корпусом	685	2200	гр. 11
ЭВ1	вывод кабеля: варочная панель — за ящиком	1135	600	гр. 8
Р27	розетка: фартук	1535	1175	гр. 7
Р32	розетка: посудомоечная машина	1685	300	гр. 10
Р26	розетка: фартук	1685	1175	рамка 2 поста, гр. 7
Р31	розетка: фартук между мойкой и варочной	1985	1175	гр. 7
Р30	розетка: фартук между мойкой и варочной	2135	1175	рамка 2 поста, гр. 7
Св49	светильник настенный	2285	1440	гр. 2, лента 785–3785 от угла
В1-6	холодная вода — посудомоечная машина	2485	550	кран ПММ в шкафу мойки
К1-6	канализация — посудомоечная машина	2585	550	Ø40; слив ПММ в шкафу мойки
Т3-3	горячая вода — мойка кухонная	2735	600	межос. 100
К1-5	канализация — мойка кухонная	2785	400	Ø50
В1-5	холодная вода — мойка кухонная	2835	600	межос. 100
Р25	розетка: холодильник — в своём модуле, над нишей, за съёмной панелью	3335	2000	гр. 11
БП5	блок питания LED: в пенале М_19, верх, съёмная панель	3485	2000	гр. 2

Условные обозначения

- розетка с заземляющим контактом; у знака — марка, ×N постов в рамке, гр. — группа щита, Н — высота оси, мм
- вывод кабеля для подключения прибора (без розетки), марка ЭВ
- светодиодная лента в профиле / в карнизе короба
- БП — блок питания LED, с доступом (люк от 100×100 мм)
- вывод В1 (код — в ведомости привязок)
- вывод Т3 (код — в ведомости привязок)
- вывод К1 (код — в ведомости привязок)
- привязки точек и выводов от угла и от пола, мм

Примечания

1. Вид «Привязки» стены В1 — электроточки и выводы ВК; архитектурная развёртка (мебель, отделка, проёмы, высоты) — на листе 64. Мебель и приборы — подложкой для ориентира; их марки и обозначения мебели, проёмов и стен — там же.
2. Привязки — в мм: по горизонтали от левого чистового угла стены до оси изделия, Н — от чистого пола до оси; все точки — в таблице привязок. Красная цепочка — привязки по осям; точки ближе 120 мм одна к другой в цепочку не дробятся — их привязки только в таблице.
3. У знака — марка электроточки (Р — розетка, S — выключатель, Св — светильник, ЭВ — вывод кабеля); условные обозначения и общие указания — лист 3.
4. Коды выводов ВК: В1 — холодная вода, Т3 — горячая вода, К1 — канализация; номер после дефиса — номер вывода на листе выводов сантехники.
5. Выводы кухонной техники — по утверждённому проекту кухни: привязки выводов даются от осей модулей гарнитура.

					Проект: Трёхкомнатная квартира — **М 1:20**
	Лист	№ док.	Подпись	Дата	Привязки электроточек и выводов ВК, стена В1. Кухня-гостиная (пом. 6)
Дизайнер	Кырлан А.С.			04.11.26	

Стадия	Лист	Листов
П	65	92

Развёртка стены А


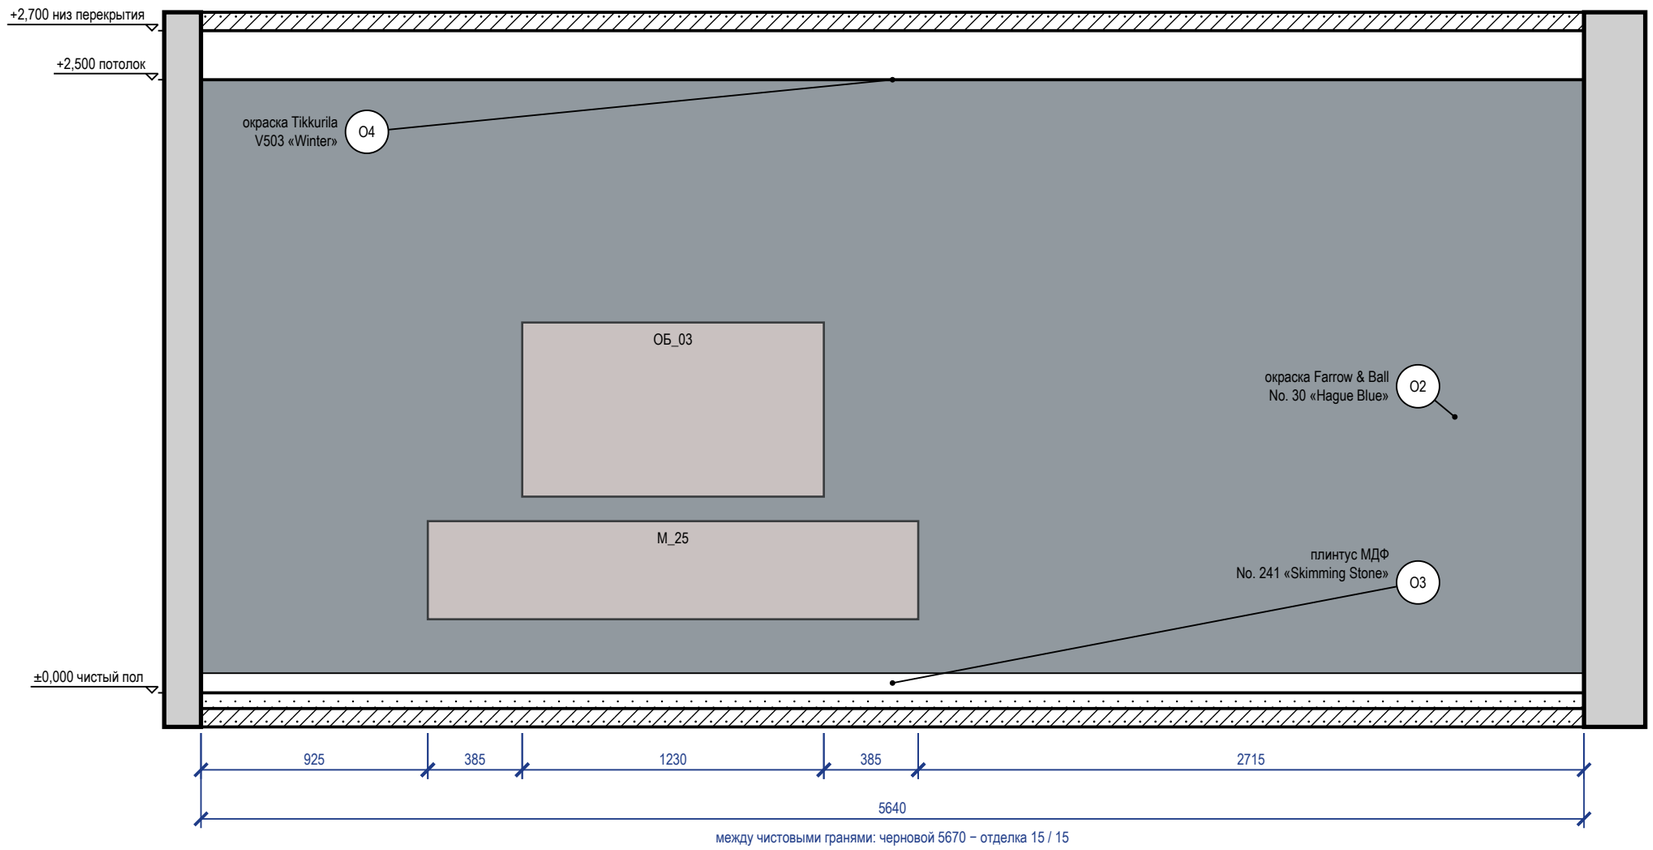


Схема развёрток (М 1:100)

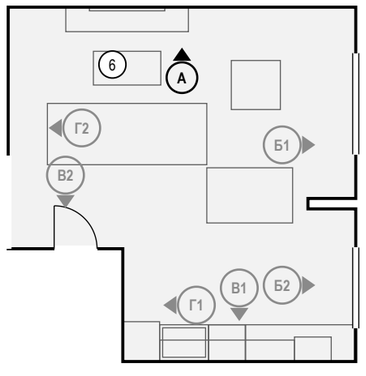

Ведомость отделки (на листе)

Марка	Поверхность	Материал, изделие	Цвет, код	Кол.
О2	акцентная стена	окраска, Farrow & Ball Modern Emulsion, матовая, подготовка Q3	Farrow & Ball No. 30 «Hague Blue»	14,1 м²
О3	плинтус	плинтус МДФ, h 80 мм, аналог: плинтус МДФ под покраску 80×16	Farrow & Ball No. 241 «Skimming Stone»	5,6 м
О4	потолок	окраска, Tikkurila Anti-Reflex 2, глубокоматовая, подготовка Q3	Tikkurila V503 «Winter»	29,2 м²

Примечания

1. Размеры — в мм от чистовых поверхностей стен; условные обозначения и общие указания — лист 3.
2. Стена А показана двумя видами: здесь — архитектурная развёртка (мебель, отделка, проёмы, высоты), электроточки и выводы ВК с привязками и таблицей — на листе 67 («Привязки»).
3. Потолок — у каждой стены свой, по плану потолков (ПТ1); ступени — зоной, кромка короба перед нишей — тонкой линией; в поле потолка: ПТ2 +2,600.

					Проект: Трёхкомнатная квартира	М 1:25
	Лист	№ док.	Подпись	Дата	Развёртка стены А. Кухня-гостиная (пом. 6)	Стадия / Лист / Листов
Дизайнер	Кырлан А.С.			04.11.26		П / 66 / 92

Развёртка стены А: электроточки и выводы

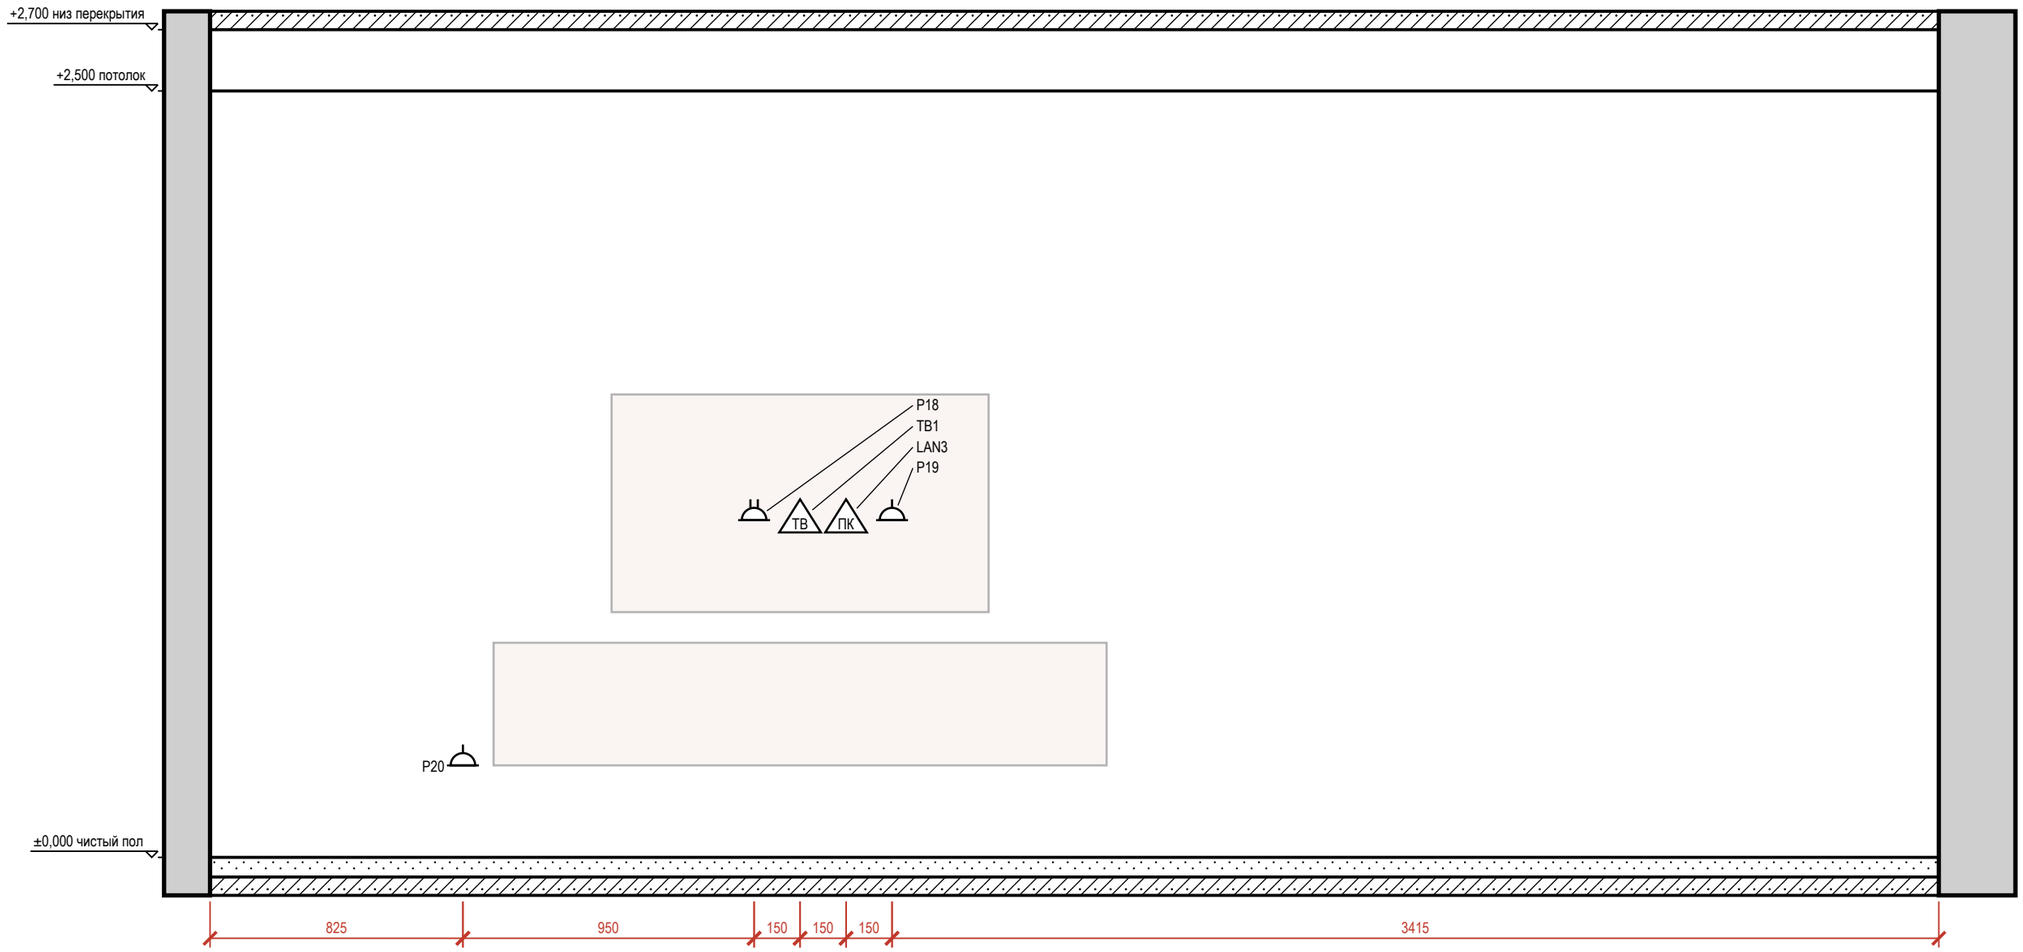



Таблица привязок электроточек и выводов

Марка	Назначение	От угла, мм	H от пола, мм	Примечание
P20	розетка: у ТВ-тумбы	825	300	гр. 6
P18	розетка: ТВ (в одной зоне с TB1, LAN3) — за экраном ОБ_03 на поворотном кронштейне, доступ при отведённом экране	1775	1100	рамка 2 поста, гр. 6
TB1	розетка ТВ: ТВ-зона — за экраном ОБ_03 на поворотном кронштейне, доступ при отведённом экране	1925	1100	
LAN3	розетка RJ45: Smart TV — за экраном ОБ_03 на поворотном кронштейне, доступ при отведённом экране	2075	1100	
P19	розетка: ТВ-приставка (в одной зоне с TB1, LAN3) — за экраном ОБ_03 на поворотном кронштейне, доступ при отведённом экране	2225	1100	гр. 6

Условные обозначения

- розетка с заземляющим контактом; у знака — марка, ×N постов в рамке, гр. — группа щита, H — высота оси, мм
- ПК — розетка компьютерная RJ45
- ТВ — розетка телевизионная
- привязки точек и выводов от угла и от пола, мм
- A — марка развёртки: буква стены, стрелка — взгляд

Схема развёрток (М 1:200)

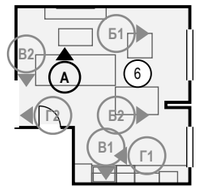

Примечания

1. Вид «Привязки» стены А — электроточки и выводы ВК; архитектурная развёртка (мебель, отделка, проёмы, высоты) — на листе 66. Мебель и приборы — подложкой для ориентира; их марки и обозначения мебели, проёмов и стен — там же.
2. Привязки — в мм: по горизонтали от левого чистового угла стены до оси изделия, H — от чистого пола до оси; все точки — в таблице привязок. Красная цепочка — привязки по осям; точки ближе 120 мм одна к другой в цепочку не дробятся — их привязки только в таблице.
3. У знака — марка электроточки (Р — розетка, S — выключатель, Св — светильник, ЭВ — вывод кабеля); условные обозначения и общие указания — лист 3.

					Проект: Трёхкомнатная квартира — М 1:20
	Лист	№ док.	Подпись	Дата	
Дизайнер	Кырлан А.С.			04.11.26	Привязки электроточек, стена А. Кухня-гостиная (пом. 6)
					Стадия: П; Лист: 67; Листов: 92

Развёртка стены Б1


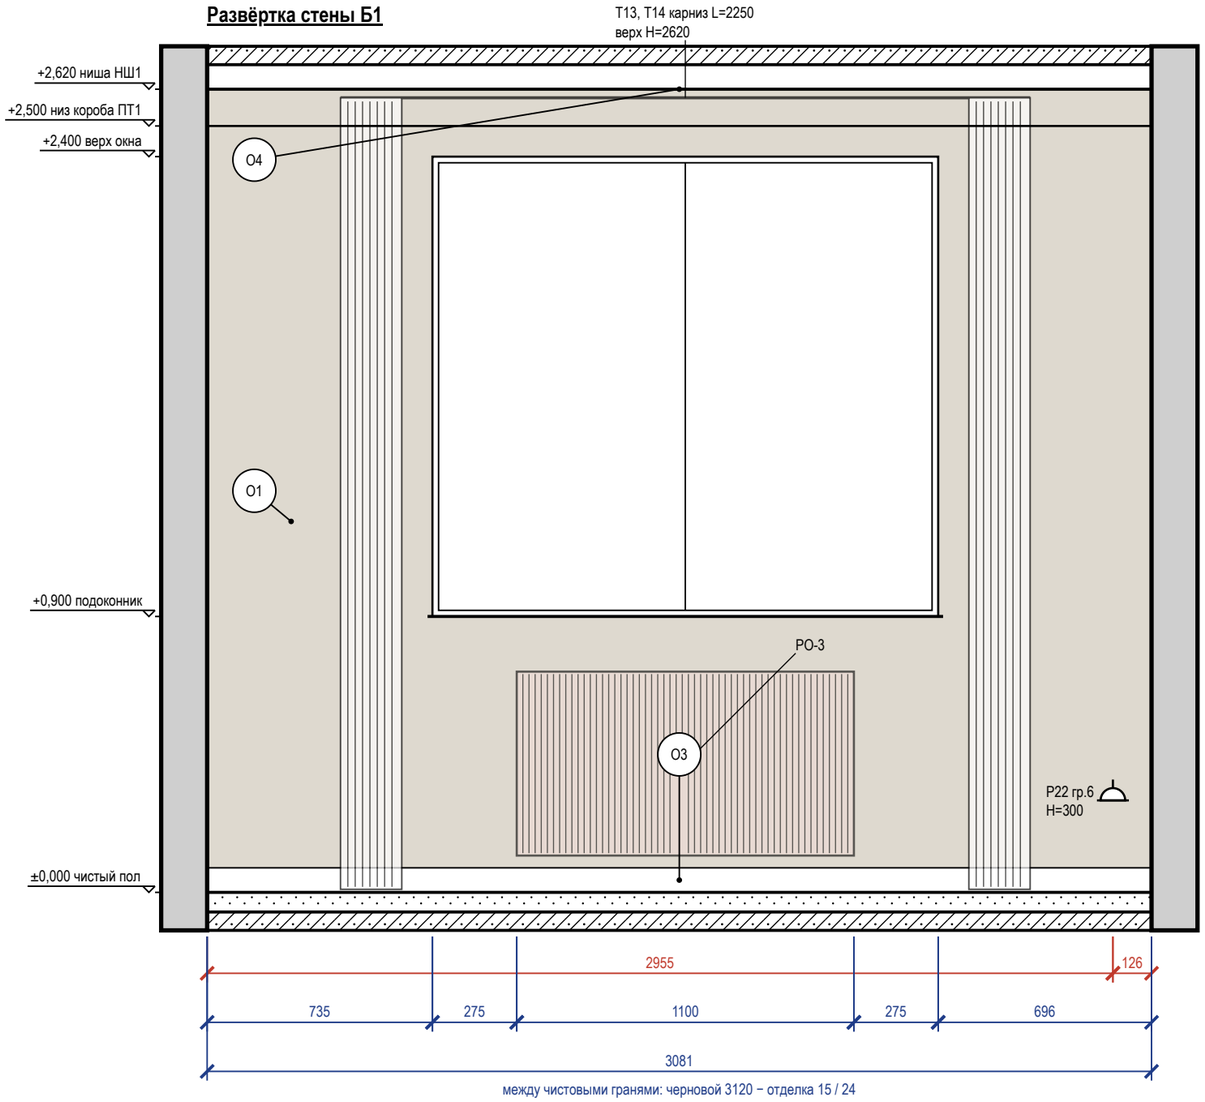


Схема развёрток (М 1:100)

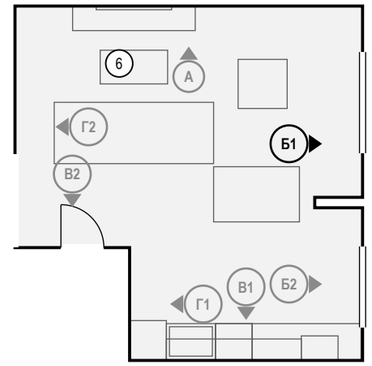

Ведомость отделки (на листе)

Марка	Поверхность	Материал, изделие	Цвет, код	Кол.
О1	стены	окраска, Farrow & Ball Modern Emulsion, матовая, подготовка Q3	Farrow & Ball No. 241 «Skimming Stone»	5,6 м²
О3	плинтус	плинтус МДФ, h 80 мм, аналог: плинтус МДФ под покраску 80×16	Farrow & Ball No. 241 «Skimming Stone»	3,1 м
О4	потолок	окраска, Tikkurila Anti-Reflex 2, глубокоматовая, подготовка Q3	Tikkurila V503 «Winter»	29,2 м²


Примечания

1. Размеры — в мм от чистовых поверхностей стен; условные обозначения и общие указания — лист 3.
2. Карнизы (шины) — по ведомости текстиля декоратора: длина L и верх H на развёртке — те же числа, что в ведомости; крепление — до окраски потолка.
3. Потолок — у каждой стены свой, по плану потолков (НШ1, ПТ1); ступени — зоной, кромка короба перед нишей — тонкой линией; в поле потолка: ПТ2 +2,600.
4. Линии узора (швы плитки, складки штор, рёбра радиаторов) прерываются у знаков и выносок — просвет между линиями не менее 0,7 мм.

					Проект: Трёхкомнатная квартира	М 1:20
	Лист	№ док.	Подпись	Дата	Развёртка стены Б1. Кухня-гостиная (пом. 6)	
Дизайнер	Кырлан А.С.			04.11.26		

Стадия	Лист	Листов
П	68	92

Развёртка стены В2

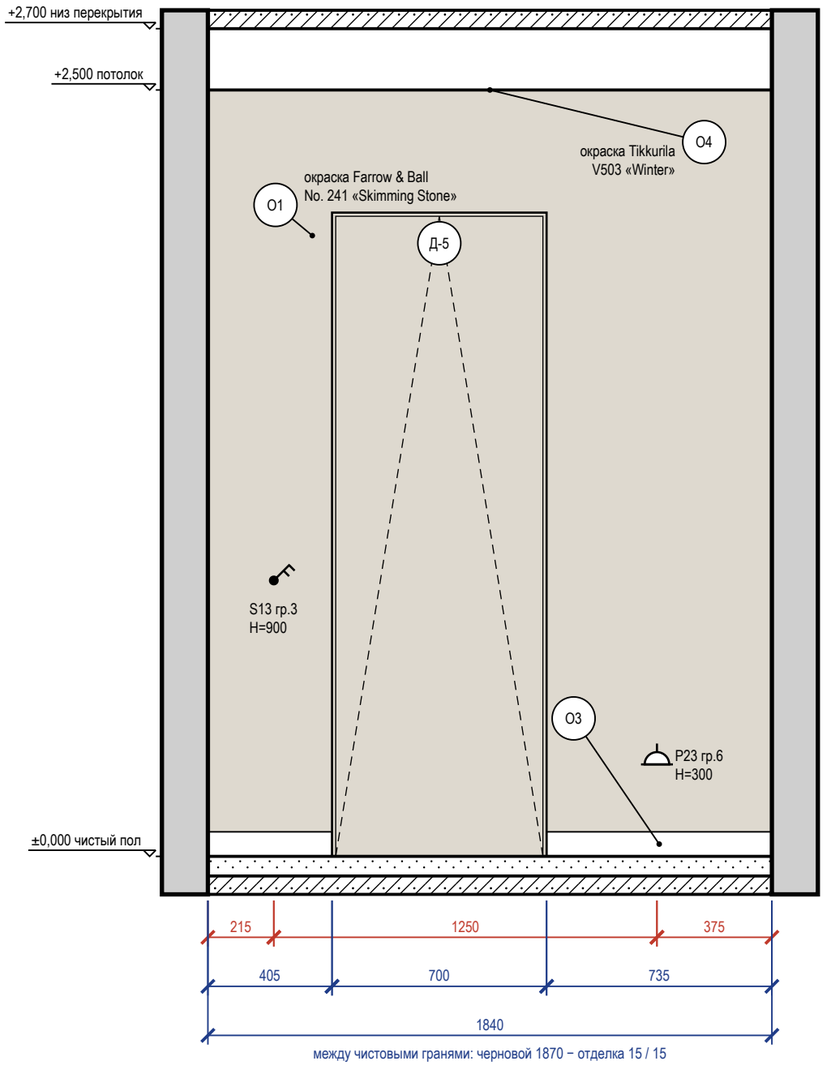

Развёртка стены Г1


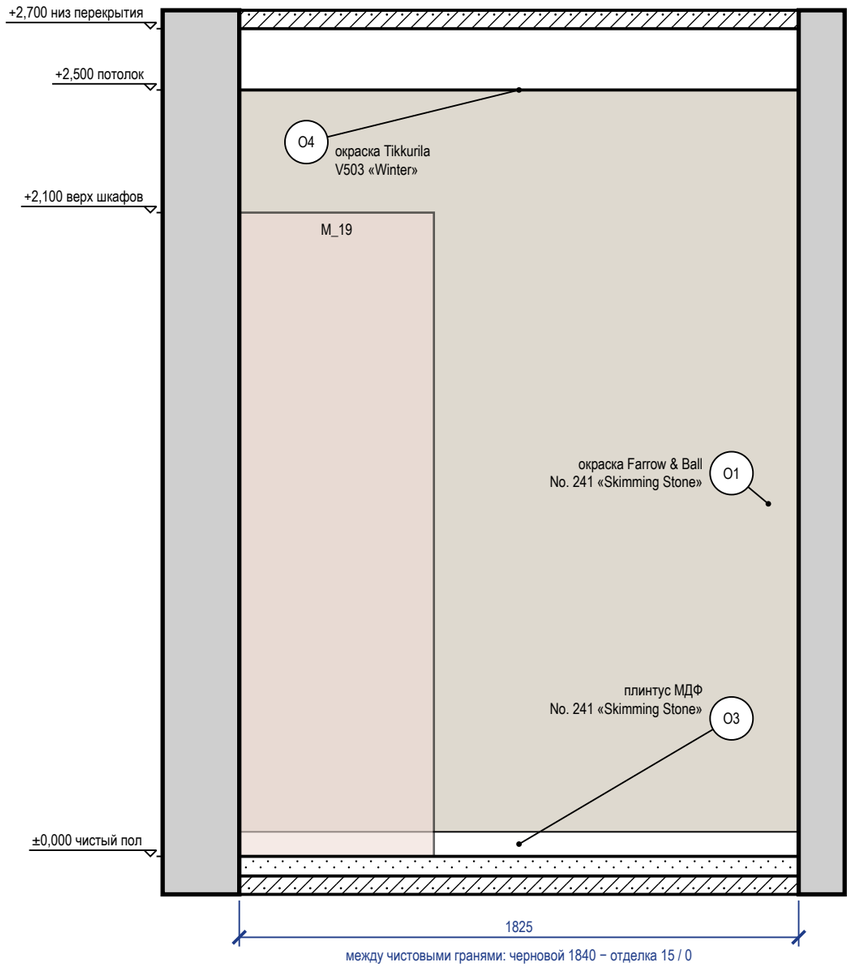


Схема развёрток (М 1:100)

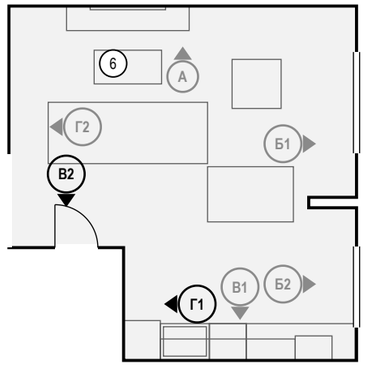

Ведомость отделки (на листе)

Марка	Поверхность	Материал, изделие	Цвет, код	Кол.
О1	стены	окраска, Farrow & Ball Modern Emulsion, матовая, подготовка Q3	Farrow & Ball No. 241 «Skimming Stone»	7,7 м²
О3	плинтус	плинтус МДФ, h 80 мм, аналог: плинтус МДФ под покраску 80×16	Farrow & Ball No. 241 «Skimming Stone»	3 м
О4	потолок	окраска, Tikkurila Anti-Reflex 2, глубокоматовая, подготовка Q3	Tikkurila V503 «Winter»	29,2 м²

Примечания

1. Размеры — в мм от чистовых поверхностей стен; условные обозначения и общие указания — лист 3.
2. Двери скрытого монтажа — полотно в плоскости стены, отделка стены по полотну, плинтус прерывается у короба (узел — на листе узлов).
3. Потолок — у каждой стены свой, по плану потолков (ПТ1); ступени — зоной, кромка короба перед нишей — тонкой линией; в поле потолка: ПТ2 +2,600.

					Проект: Трёхкомнатная квартира — М 1:20
	Лист	№ док.	Подпись	Дата	
Дизайнер	Кырлан А.С.			04.11.26	Развёртки стен В2, Г1. Кухня-гостиная (пом. 6)
					Стадия: П; Лист: 69; Листов: 92

Развёртка стены Г2


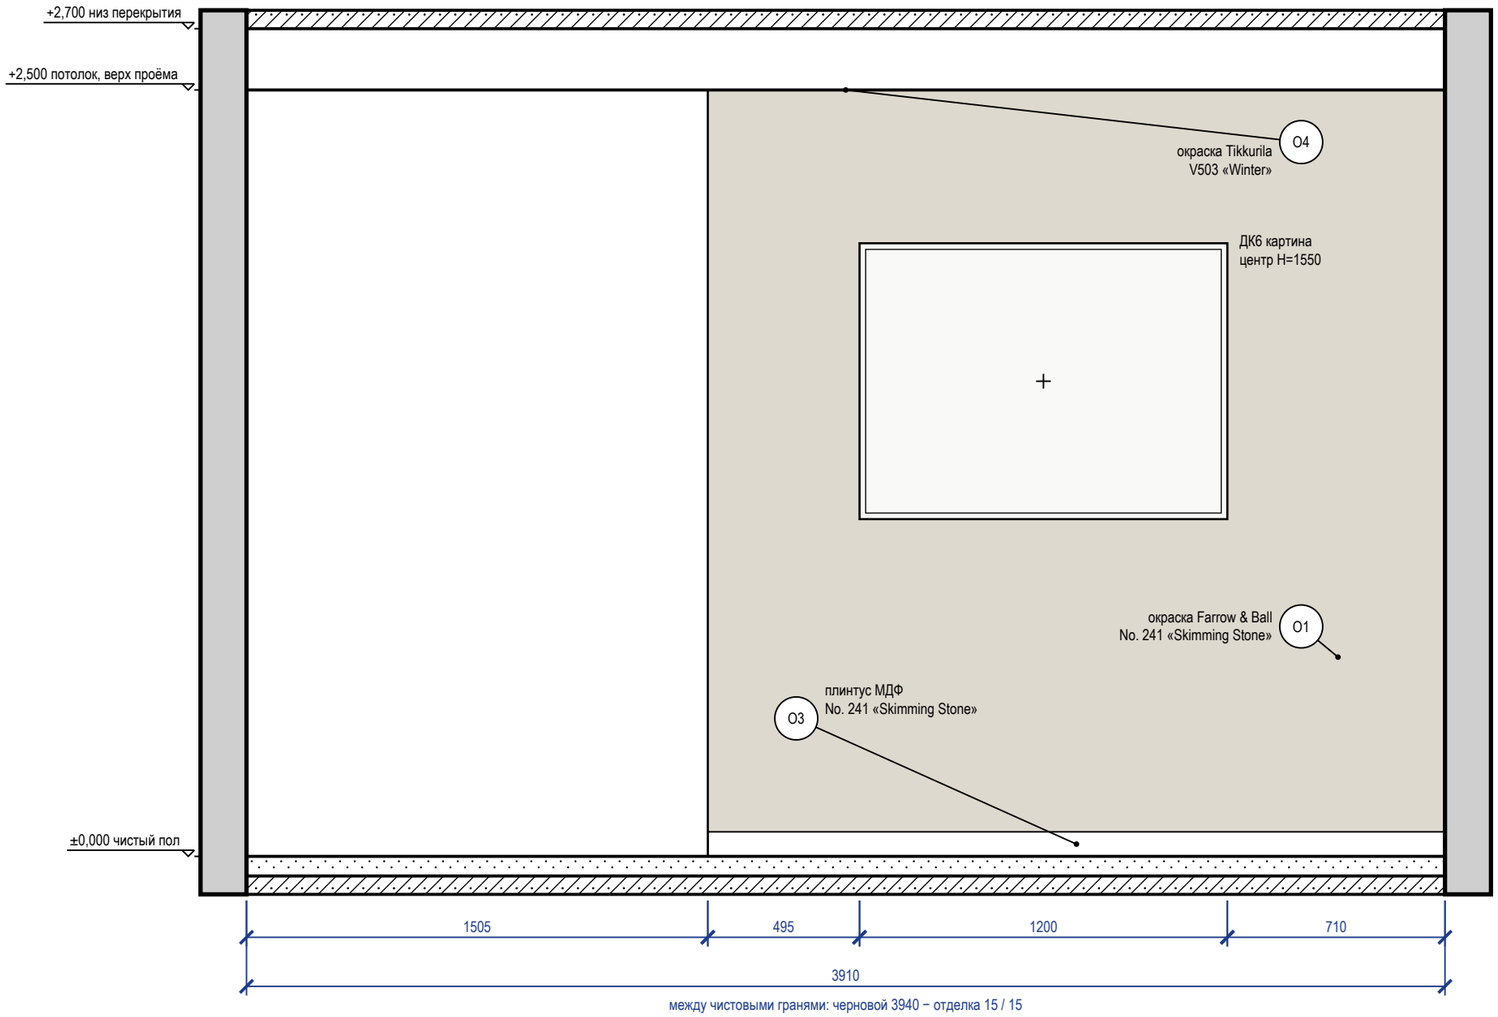


Схема развёрток (М 1:100)

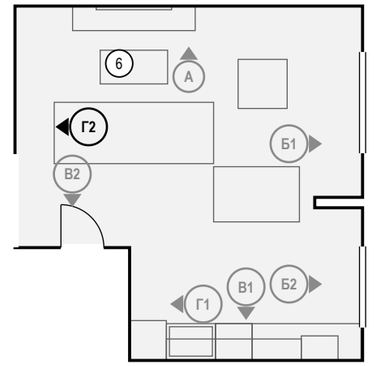

Ведомость отделки (на листе)

Марка	Поверхность	Материал, изделие	Цвет, код	Кол.
О1	стены	окраска, Farrow & Ball Modern Emulsion, матовая, подготовка Q3	Farrow & Ball No. 241 «Skimming Stone»	6 м²
О3	плинтус	плинтус МДФ, h 80 мм, аналог: плинтус МДФ под покраску 80×16	Farrow & Ball No. 241 «Skimming Stone»	2,4 м
О4	потолок	окраска, Tikkurila Anti-Reflex 2, глубокоматовая, подготовка Q3	Tikkurila V503 «Winter»	29,2 м²

Примечания

1. Размеры — в мм от чистовых поверхностей стен; условные обозначения и общие указания — лист 3.
2. Стена Г2 показана двумя видами: здесь — архитектурная развёртка (мебель, отделка, проёмы, высоты), электроточки и выводы ВК с привязками и таблицей — на листе 71 («Привязки»).
3. Картины и зеркала крепить к основанию по паспорту изделия (закладные и анкеры — в перечне скрытых работ); крест — ось центра предмета.
4. Потолок — у каждой стены свой, по плану потолков (ПТ1); ступени — зоной, кромка короба перед нишей — тонкой линией; в поле потолка: ПТ2 +2,600.

					Проект: Трёхкомнатная квартира	М 1:20
	Лист	№ док.	Подпись	Дата		
Дизайнер	Кырлан А.С.			04.11.26	Развёртка стены Г2. Кухня-гостиная (пом. 6)	Стадия: П; Лист: 70; Листов: 92

Развёртка стены Г2: электроточки и выводы

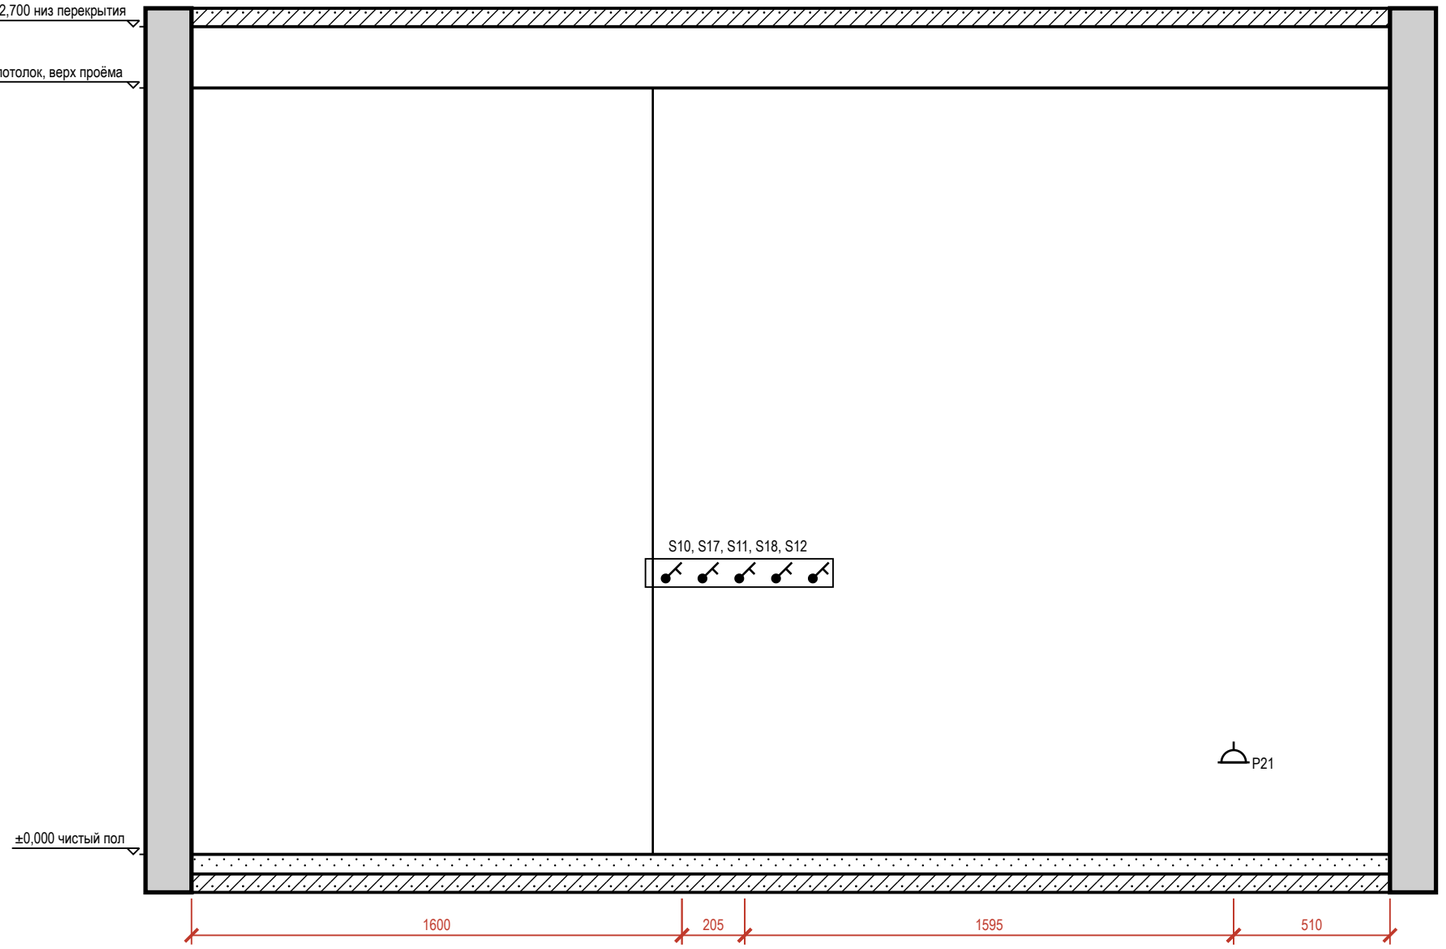


Таблица привязок электроточек и выводов

Марка	Назначение	От угла, мм	H от пола, мм	Примечание
S10	выключатель	1600	900	гр. 2
S17	выключатель	1680	900	гр. 2
S11	выключатель	1805	900	гр. 2
S18	выключатель	1885	900	гр. 2
S12	выключатель	1965	900	гр. 2
P21	розетка: торшер	3400	300	гр. 6

Условные обозначения

- розетка с заземляющим контактом; у знака — марка, ×N постов в рамке, гр. — группа щита, H — высота оси, мм
- выключатель одноклавишный
- привязки точек и выводов от угла и от пола, мм
- марка развёртки: буква стены, стрелка — взгляд


Схема развёрток (М 1:50)

Примечания

1. Вид «Привязки» стены Г2 — электроточки и выводы ВК; архитектурная развёртка (мебель, отделка, проёмы, высоты) — на листе 70. Мебель и приборы — подложкой для ориентира; их марки и обозначения мебели, проёмов и стен — там же.
2. Привязки — в мм: по горизонтали от левого чистового угла стены до оси изделия, H — от чистого пола до оси; все точки — в таблице привязок. Красная цепочка — привязки по осям; точки ближе 120 мм одна к другой в цепочку не дробятся — их привязки только в таблице.
3. У знака — марка электроточки (P — розетка, S — выключатель, Св — светильник, ЭВ — вывод кабеля); условные обозначения и общие указания — лист 3.


					Проект: Трёхкомнатная квартира	М 1:20
	Лист	№ док.	Подпись	Дата		
Дизайнер	Кырлан А.С.			04.11.26	Привязки электроточек, стена Г2. Кухня-гостиная (пом. 6)	Стадия: П; Лист: 71; Листов: 92

Развёртка стены А

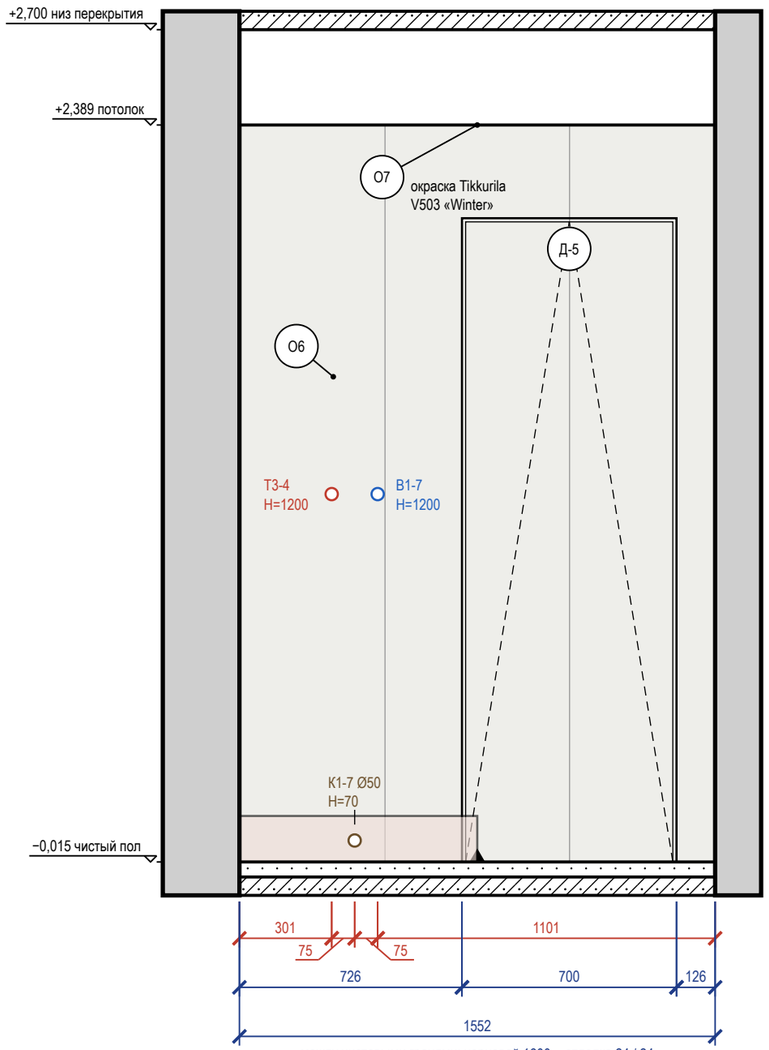


между чистовыми гранями: черновой 1600 − отделка 24 / 24

Развёртка стены Б

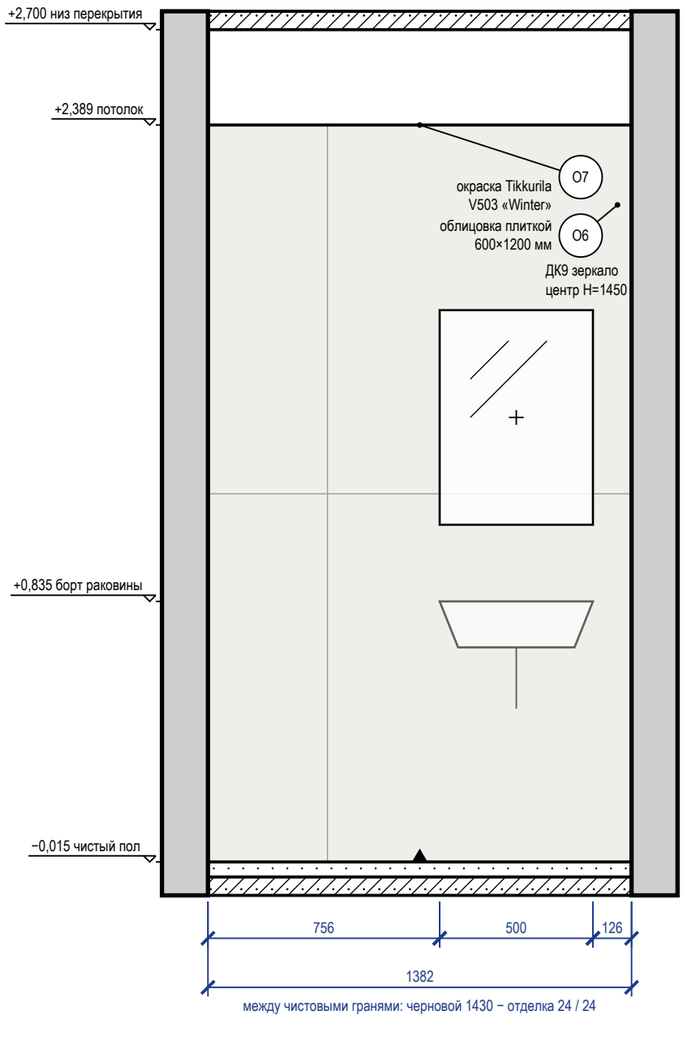


между чистовыми гранями: черновой 1430 − отделка 24 / 24

Развёртка стены В

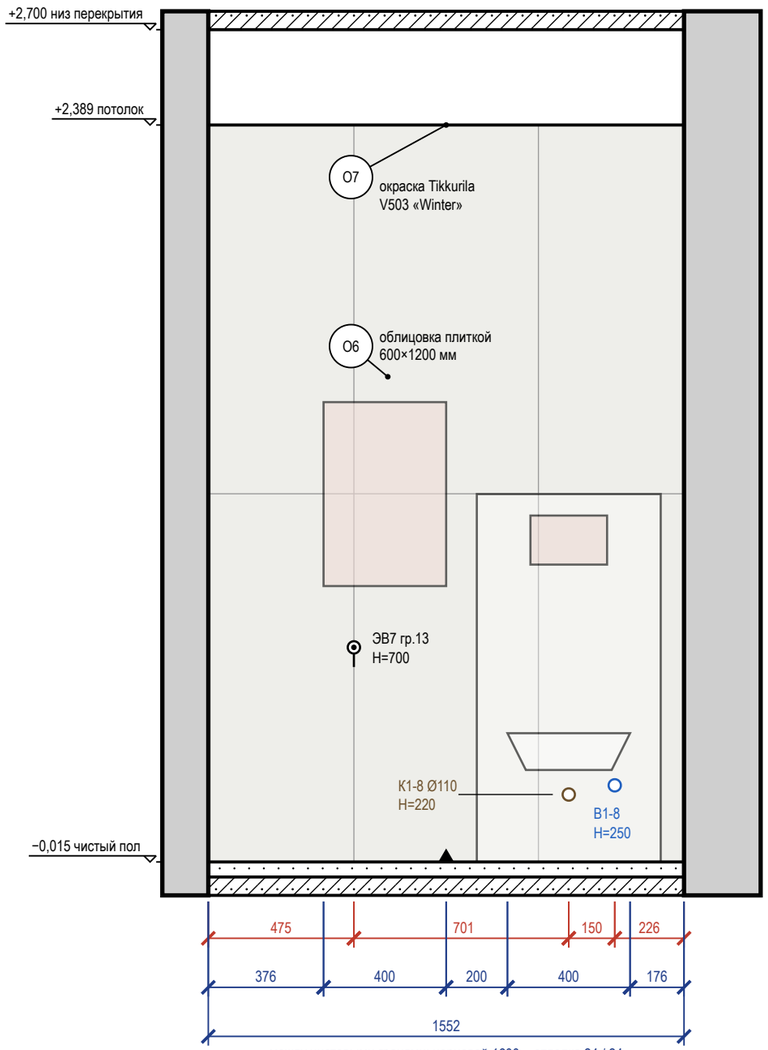

между чистовыми гранями: черновой 1600 − отделка 24 / 24

Схема развёрток (М 1:100)

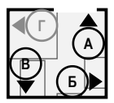

Ведомость отделки (на листе)

Марка	Поверхность	Материал, изделие	Цвет, код	Кол.
О6	стены	облицовка плиткой, 600×1200×9 мм, аналог: керамогранит под травертин, матовый, затирка CG2WA		9,3 м²
О7	потолок	окраска, Tikkurila Luja 7, матовая, подготовка Q3	Tikkurila V503 «Winter»	2,3 м²

Примечания

1. Размеры — в мм от чистовых поверхностей стен; условные обозначения и общие указания — лист 3.
2. Стена Б показана двумя видами: здесь — архитектурная развёртка (мебель, отделка, проёмы, высоты), электроточки и выводы ВК с привязками и таблицей — на листе 73 («Привязки»).
3. Схема мебели, приборов и декора не является технической документацией для производства мебели; габариты — по паспортам изделий.
4. Выводы ВК — коды и высоты по листу выводов сантехники.
5. Облицовка — по сетке швов 2 мм, раскладка от оси стены (треугольник у пола), целые ряды от пола; подрезки — по листу раскладки плитки.
6. Гидроизоляция в 2 слоя, заход на стены 200 мм; у душа — до 2000 и 500 мм за поддон — до облицовки, с актом скрытых работ и тестом проливом (узел — на листе узлов).
7. Картины и зеркала крепить к основанию по паспорту изделия (закладные и анкеры — в перечне скрытых работ); крест — ось центра предмета.
8. Двери скрытого монтажа — полотно в плоскости стены, отделка стены по полотну, плинтус прерывается у короба (узел — на листе узлов).

					Проект: Трёхкомнатная квартира — М 1:20
	Лист	№ док.	Подпись	Дата	Развёртки стен А, Б, В. Санузел 2 (пом. 7)
Дизайнер	Кырлан А.С.			04.11.26	

Стадия	Лист	Листов
П	72	92

Развёртка стены Б: электроточки и выводы

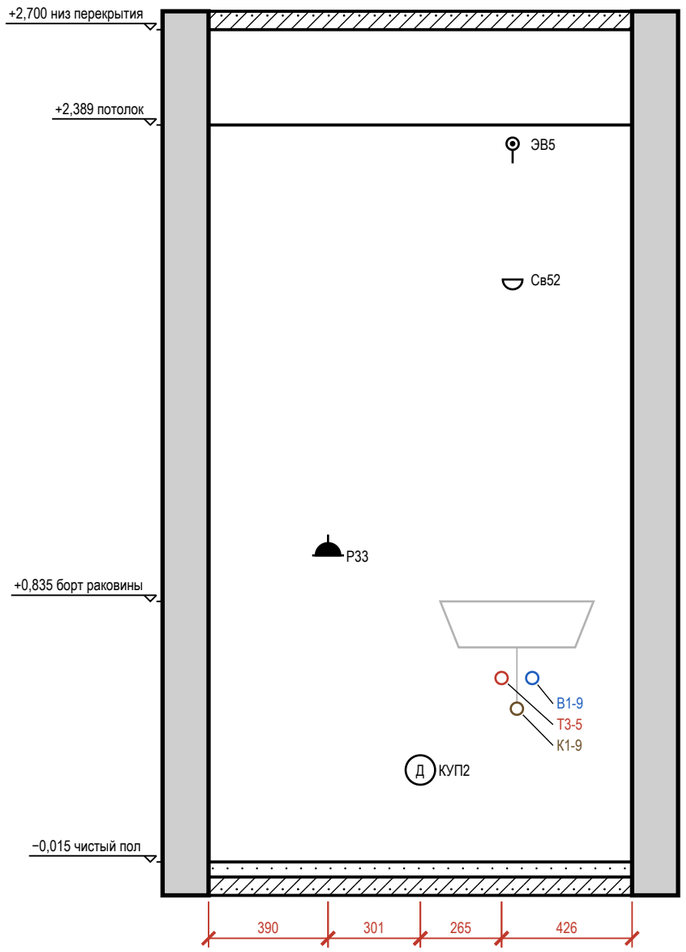



Таблица привязок электроточек и выводов

Марка	Назначение	От угла, мм	Н от пола, мм	Примечание
Р33	розетка: фен у умывальника	390	1000	гр. 13, IP44
КУП2	КУП — уравнивание потенциалов (ДСУП)	691	300	
Т3-5	горячая вода — умывальник	956	600	межос. 100
Св52	светильник настенный	992	1900	гр. 3
ЭВ5	вывод кабеля: вентилятор ВР3 (таймер выбега)	992	2343	гр. 3
К1-9	канализация — умывальник	1006	500	Ø50
В1-9	холодная вода — умывальник	1056	600	межос. 100

Условные обозначения

- розетка влагозащищённая IP44
- вывод кабеля для подключения прибора (без розетки), марка ЭВ
- светильник настенный (бра), Н — высота оси
- вывод В1 (код — в ведомости привязок)
- вывод Т3 (код — в ведомости привязок)
- вывод К1 (код — в ведомости привязок)
- привязки точек и выводов от угла и от пола, мм
- марка развёртки: буква стены, стрелка — взгляд

Схема развёрток (М 1:50)

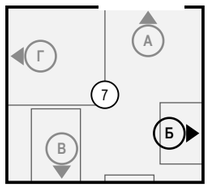

Примечания

1. Вид «Привязки» стены Б — электроточки и выводы ВК; архитектурная развёртка (мебель, отделка, проёмы, высоты) — на листе 72. Мебель и приборы — подложкой для ориентира; их марки и обозначения мебели, проёмов и стен — там же.
2. Привязки — в мм: по горизонтали от левого чистового угла стены до оси изделия, Н — от чистого пола до оси; все точки — в таблице привязок. Красная цепочка — привязки по осям; точки ближе 120 мм одна к другой в цепочку не дробятся — их привязки только в таблице.
3. У знака — марка электроточки (Р — розетка, S — выключатель, Св — светильник, ЭВ — вывод кабеля); условные обозначения и общие указания — лист 3.
4. Коды выводов ВК: В1 — холодная вода, Т3 — горячая вода, К1 — канализация; номер после дефиса — номер вывода на листе выводов сантехники.

					Проект: Трёхкомнатная квартира	М 1:20
	Лист	№ док.	Подпись	Дата		
Дизайнер	Кырлан А.С.			04.11.26	Привязки электроточек и выводов ВК, стена Б. Санузел 2 (пом. 7)	Стадия: П; Лист: 73; Листов: 92

Развёртка стены Г


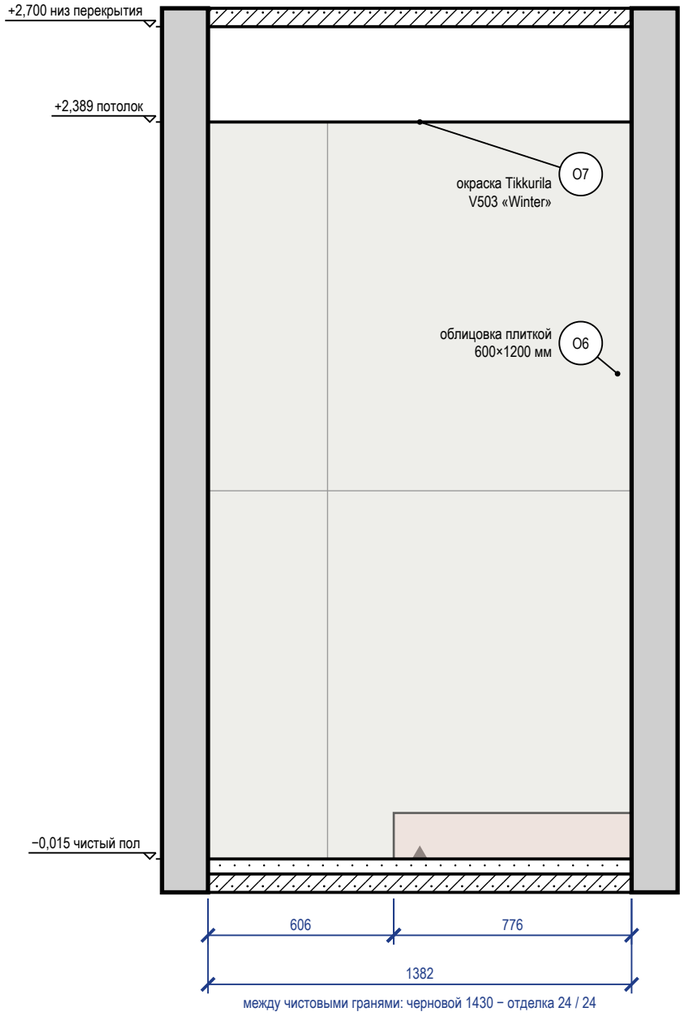


Схема развёрток (М 1:100)

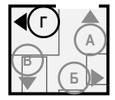

Ведомость отделки (на листе)


Марка	Поверхность	Материал, изделие	Цвет, код	Кол.
О6	стены	облицовка плиткой, 600×1200×9 мм, аналог: керамогранит под травертин, матовый, затирка CG2WA		3,3 м²
О7	потолок	окраска, Tikkurila Luja 7, матовая, подготовка Q3	Tikkurila V503 «Winter»	2,3 м²

Примечания

1. Размеры — в мм от чистовых поверхностей стен; условные обозначения и общие указания — лист 3.
2. Схема мебели, приборов и декора не является технической документацией для производства мебели; габариты — по паспортам изделий.
3. Облицовка — по сетке швов 2 мм, раскладка от оси стены (треугольник у пола), целые ряды от пола; подрезки — по листу раскладки плитки.
4. Гидроизоляция в 2 слоя, заход на стены 200 мм; у душа — до 2000 и 500 мм за поддон — до облицовки, с актом скрытых работ и тестом проливом (узел — на листе узлов).

					Проект: Трёхкомнатная квартира	М 1:20
	Лист	№ док.	Подпись	Дата		
Дизайнер	Кырлан А.С.			04.11.26	Развёртка стены Г. Санузел 2 (пом. 7)	Стадия: П; Лист: 74; Листов: 92

Развёртка стены А

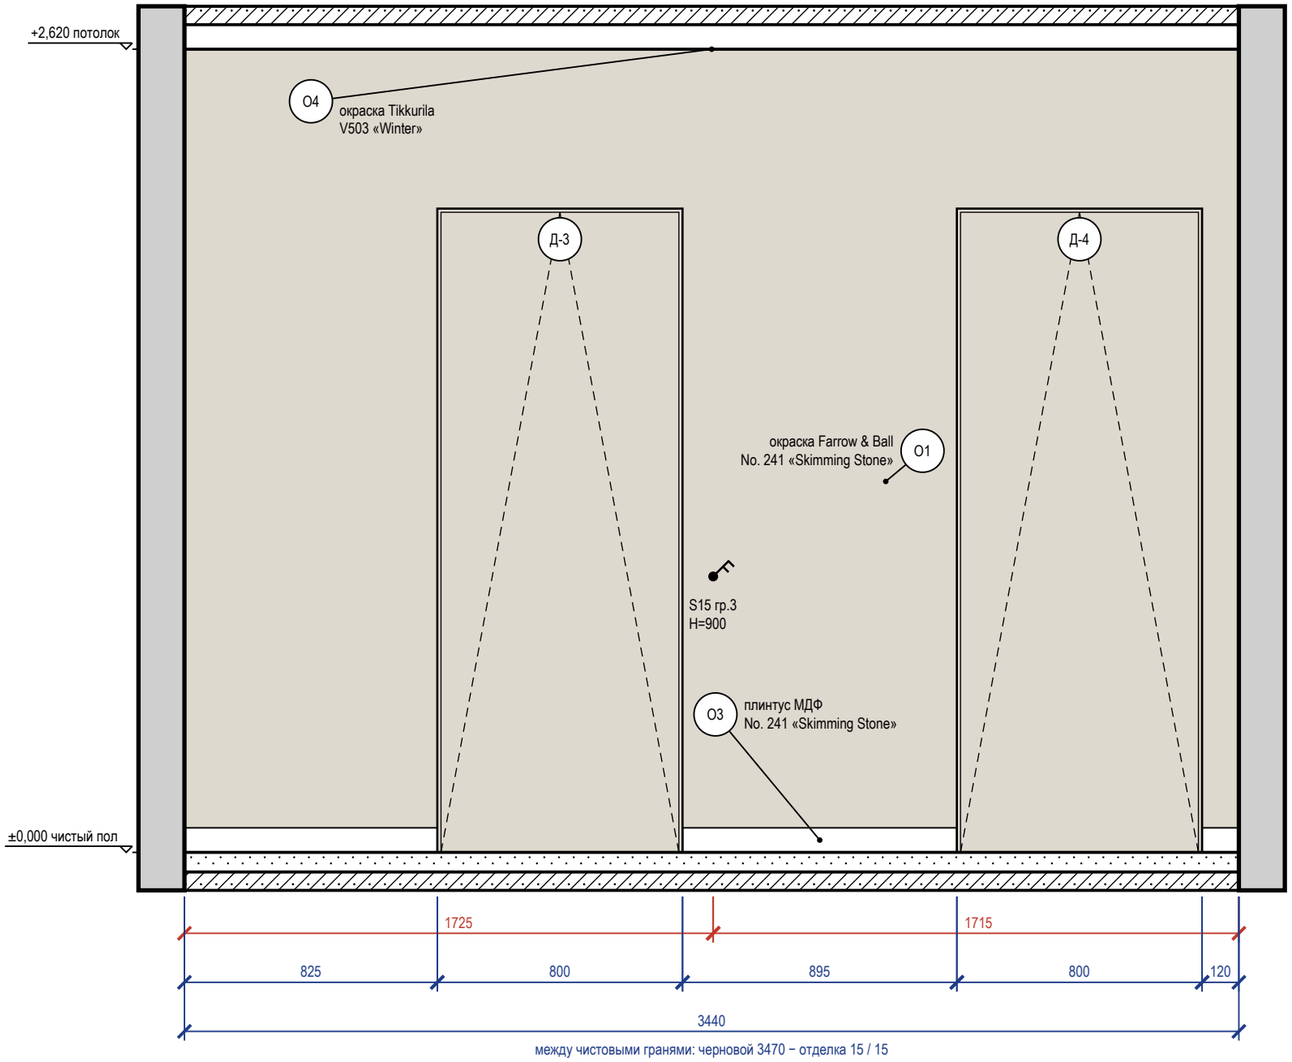

Развёртка стены Б


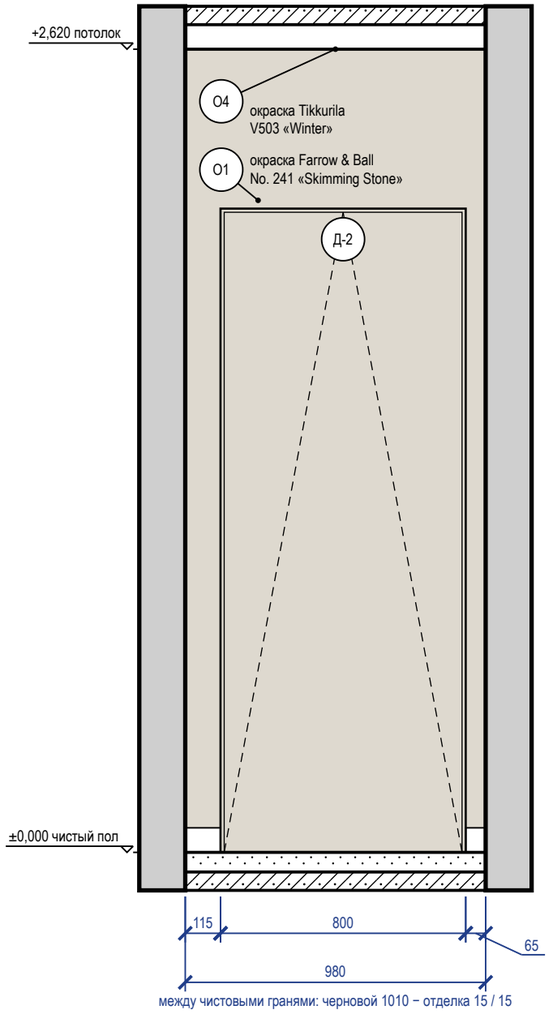


Схема развёрток (М 1:100)

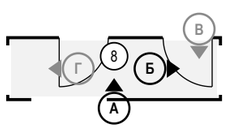

Ведомость отделки (на листе)

Марка	Поверхность	Материал, изделие	Цвет, код	Кол.
О1	стены	окраска, Farrow & Ball Modern Emulsion, матовая, подготовка Q3	Farrow & Ball No. 241 «Skimming Stone»	6,5 м²
О3	плинтус	плинтус МДФ, h 80 мм, аналог: плинтус МДФ под покраску 80×16	Farrow & Ball No. 241 «Skimming Stone»	2 м
О4	потолок	окраска, Tikkurila Anti-Reflex 2, глубокоматовая, подготовка Q3	Tikkurila V503 «Winter»	3,5 м²

Примечания

1. Размеры — в мм от чистовых поверхностей стен; условные обозначения и общие указания — лист 3.
2. Двери скрытого монтажа — полотно в плоскости стены, отделка стены по полотну, плинтус прерывается у короба (узел — на листе узлов).


	Лист	№ док.	Подпись	Дата
Дизайнер	Кырлан А.С.			04.11.26

Проект: Трёхкомнатная квартира — М 1:20

Развёртки стен А, Б. Коридор (пом. 8)


Стадия	Лист	Листов
П	75	92

Развёртка стены В

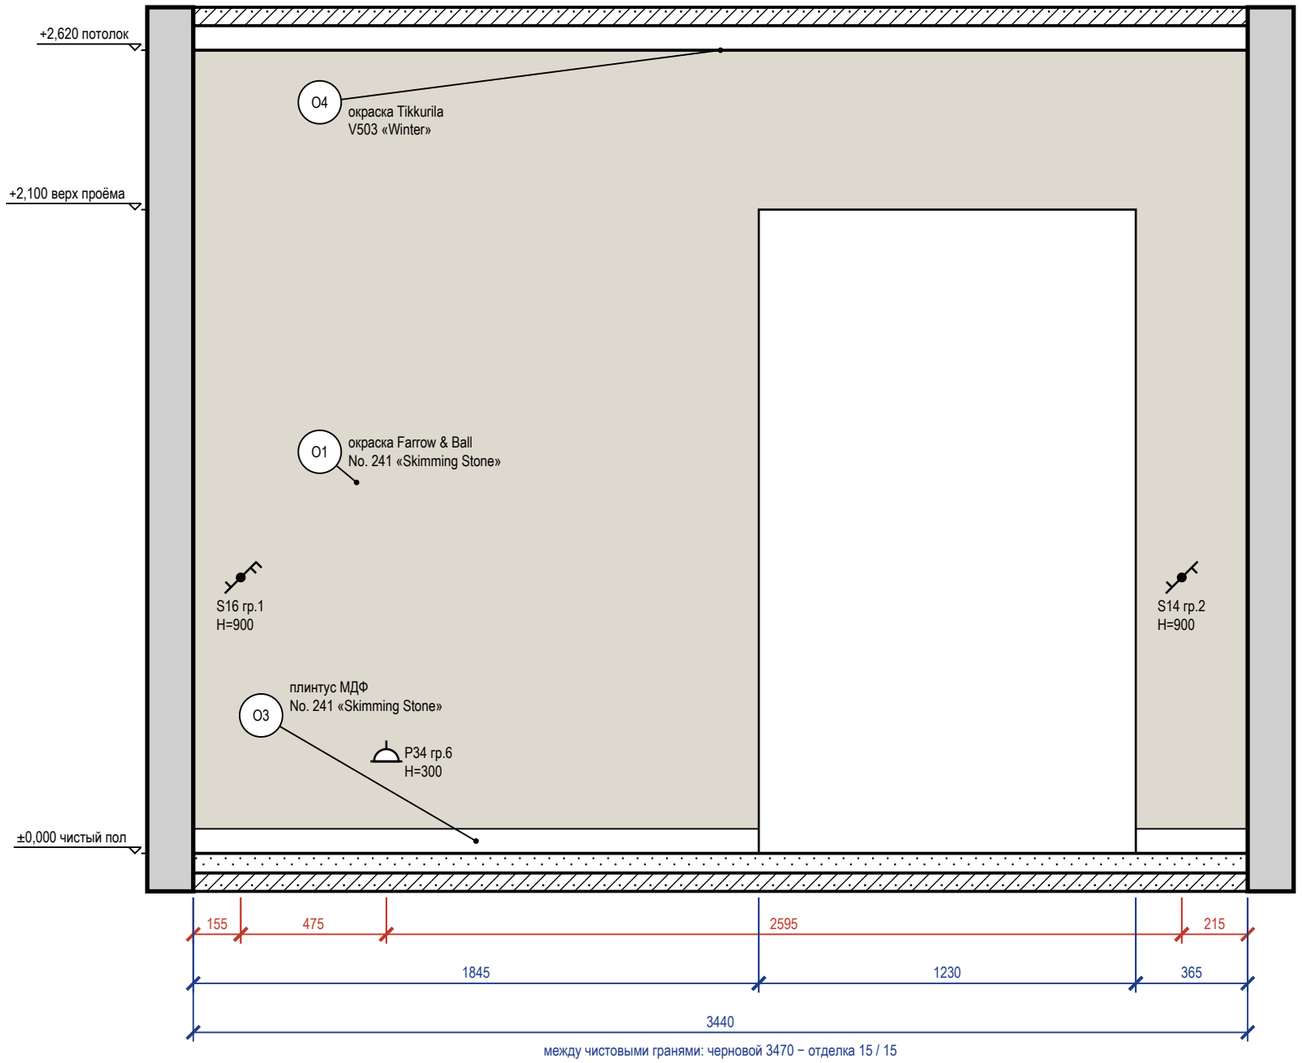


между чистовыми гранями: черновой 3470 − отделка 15 / 15

Развёртка стены Г

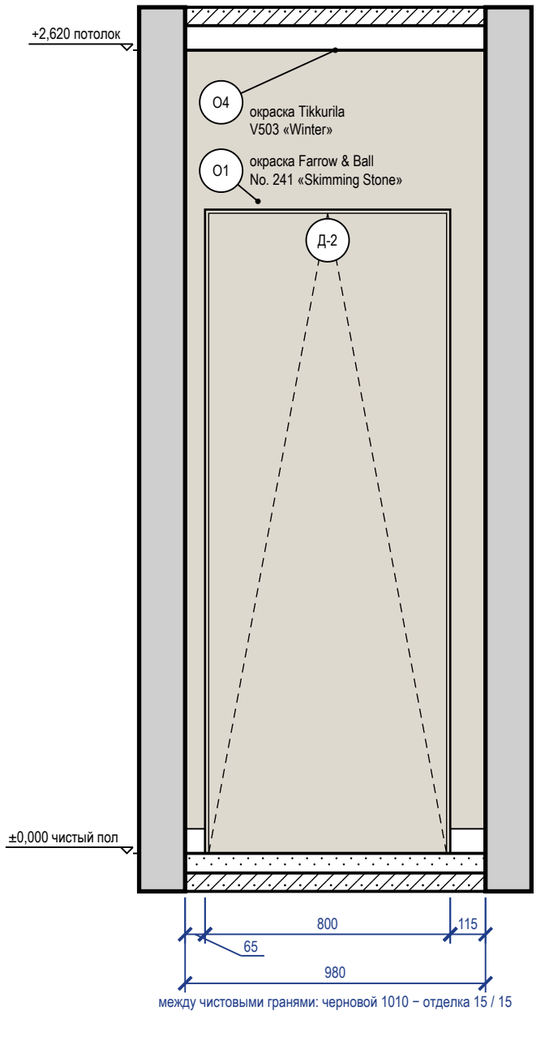

между чистовыми гранями: черновой 1010 − отделка 15 / 15

Схема развёрток (М 1:100)

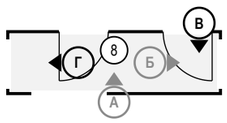

Ведомость отделки (на листе)

Марка	Поверхность	Материал, изделие	Цвет, код	Кол.
О1	стены	окраска, Farrow & Ball Modern Emulsion, матовая, подготовка Q3	Farrow & Ball No. 241 «Skimming Stone»	7,3 м²
О3	плинтус	плинтус МДФ, h 80 мм, аналог: плинтус МДФ под покраску 80×16	Farrow & Ball No. 241 «Skimming Stone»	2,4 м
О4	потолок	окраска, Tikkurila Anti-Reflex 2, глубокоматовая, подготовка Q3	Tikkurila V503 «Winter»	3,5 м²

Примечания

1. Размеры — в мм от чистовых поверхностей стен; условные обозначения и общие указания — лист 3.
2. Двери скрытого монтажа — полотно в плоскости стены, отделка стены по полотну, плинтус прерывается у короба (узел — на листе узлов).

					Проект: Трёхкомнатная квартира	М 1:20
	Лист	№ док.	Подпись	Дата		
Дизайнер	Кырлан А.С.			04.11.26	Развёртки стен В, Г. Коридор (пом. 8)	Стадия: П; Лист: 76; Листов: 92

Комплект предварительный по пунктам этих таблиц. Пока по пункту нет ответа или решения, показанное на указанном листе — допущение проектировщика, а не утверждённое решение.
Сводка: открытых вопросов — 27 (из них ждут факта объекта — 17: контрольного обмера, обследования или документа); изменений в реестре — 18, из них без подписи — 6.

Открытые вопросы и принятые допущения

№	Формулировка	Вид	Кто решает	Если решения нет	Лист, где это проявляется
К-1	Ванная (2250 × 1970 мм): после утверждения стиральной машины с вертикальной загрузкой 400 × 600 мм (ИЗ-11) замечания по дверце машины и боковому зазору унитаза С_02 сняты. Остаются: в зоне 750 мм перед ванной С_01 стоит умывальник С_03; розетка Р7 в 348 мм от стояка (нужно 500). Предложение, в проект не принято: умывальник С_03 развернуть до 600 × 450 мм к стене В, унитаз С_02 сдвинуть на 150 мм, розетки Р7 и Р8, светильник и зеркало перенести по новой раскладке. Решить: принять предложение, оставить как есть с открытыми замечаниями или предложить другую раскладку.	Спорно Ждёт: решения	Инженер ВК (вода, канализация)	в проекте остаются умывальник С_03 в зоне перед ванной и розетка Р7 в 348 мм от стояка; эти отступления остаются открытыми	л. 17 — План выводов сантехники л. 35 — План розеток и электровыводов
К-2	Артикул плитки и калибр партии (фактический размер плитки) для ванной и санузла 2 не заданы: раскладка рассчитана по номинальным размерам — пол 600 × 600 мм, стены 600 × 1200 мм. Требование к закупке: выбрать плитку и до раскладки измерить калибр на образце партии (или взять из паспорта партии); раскладку пересчитать по измеренному калибру до заказа плитки и до укладки. Пока калибр не измерен, подрезка у стен и число плиток по листам раскладки — расчётные.	Отсутствует Ждёт: данных закупки, затем решения	Плиточник	раскладка остаётся по номинальным размерам; подрезку у стен определять по фактической партии, раскладку пересчитать по измеренному калибру	л. 43 — Раскладка плитки. Планы полов л. 27 — Раскладка плитки. Ванная. Развёртки стен л. 28 — Раскладка плитки. Санузел 2. Развёртки стен
К-3	Доли цвета по поверхностям не укладываются в схему 60/30/10 и её варианты: ведущий цвет занимает 33 % в спальне 1, 38 % в спальне 2 и 32 % в кухне-гостиной (нужно от 50 %); акцент в спальне 1 — 19 %, в спальне 2 — 18 % (больше 15 %); в гардеробной ведущий цвет занимает 90 % (больше 80 %), второй цвет почти не читается. Решить, какие поверхности считать ведущим цветом в каждой комнате, или принять распределение как есть.	Спорно Ждёт: решения	Колорист-комплектатор	цвета остаются в показанных долях, ведущий цвет в трёх комнатах не определён	л. 11 — Колерная карта
К-4	Вход в санузел 2 (с унитазом) — из кухни-гостиной: так по плану заказчика (ниша у входа на плане открыта в кухню-гостиную, в проекте закрыта перегородкой по линии низа прихожей). Вход в помещение с унитазом принято устраивать из коридора или прихожей. Принять существующее положение или перепланировать вход.	Спорно Ждёт: решения	Архитектор-планировщик	Остаётся вариант, показанный на листе; он не утверждён, лист предварительный.	л. 5 — План планировки от заказчика л. 29 — План размещения дверей
К-5	Санузел 2 (1675 × 1580 мм): перед душем С_06 до противоположной стены 630 мм (нужно 750); зону перед унитазом С_07 и умывальником С_08 занимает сам поддон душа С_06; боковой зазор умывальника С_08 — 150 мм (нужно 200). Принять как проектное решение «перекрытие зон движения» нельзя: VDI 6000 допускает перекрытие зон движения соседних приборов, но не прибор в зоне движения другого, а здесь в зоне стоит поддон душа, и глубина перед душем меньше 750 мм. Отступление от этой зарубежной рекомендации (в российских нормах размеры перед приборами не заданы) возможно только как осознанный отказ от неё при малом помещении либо перестановкой приборов.	Спорно Ждёт: решения	Инженер ВК (вода, канализация)	приборы остаются как показаны: поддон душа стоит в зоне перед унитазом и умывальником, глубина перед душем 630 мм; отступление не принято и не обосновано	л. 17 — План выводов сантехники
К-7	Розетки выше 1 м от пола (норма ПУЭ, п. 6.6.30 — не выше 1 м). Р7 (стиральная машина) и Р8 (фен) в ванной стояли на 1200 мм, Р33 (фен, санузел 2) — на 1100 мм: назначение не требует такой высоты, розетки опущены до 1000 мм (запись ИЗ-9). Остаются выше 1 м по назначению, основание записано в самой позиции (знак «**» у марки, примечание листа, графа «Назначение» ведомости): Р12 (ТВ над комодом, спальня 2) — 1100 мм, питание телевизора на стене, в одной зоне с ТВ2 и LAN2; Р18 (ТВ) и Р19 (ТВ-приставка, кухня-гостиная) — 1100 мм, в одной зоне с ТВ1 и LAN3; Р17 (питание слаботочного щита ЩС, прихожая) — 1700 мм, рядом со щитом на его высоте; Р25 (холодильник) — 2000 мм, над нишей М_19 за съёмной панелью. Подтвердить высоты или опустить розетки.	Спорно Ждёт: решения	Инженер-электрик	высоты остаются как на листе, решение не подтверждено	л. 35 — План розеток и электровыводов полный альбом
К-8	Проект кухни не утверждён заказчиком: выводы кухонной техники (мойка М_20, посудомоечная М_21, варочная панель и духовой шкаф М_22, вытяжка М_24, холодильник М_19) приняты по типовой расстановке техники. Раскладка гарнитура принята автором проектной (ИЗ-12) с условием: до начала черновых работ сверить её и выводы техники с чертежом кухни от изготовителя гарнитура; чертёж изготовителя нужно получить и передать. Пока чертежа нет, привязки выводов даны от осей модулей гарнитура и пересматриваются вместе с проектом кухни.	Отсутствует Ждёт: документа, обмера, затем решения	Мебельщик	выводы остаются привязанными к раскладке гарнитура, принятой проектной и не сверенной с чертежом изготовителя	л. Д_4 — Кухня (пом. 6). Развёртка гарнитура л. 35 — План розеток и электровыводов
К-9	Гардеробная состоит из двух частей; проход между ними через стык — 280 мм (нужно 700 мм), он сужает систему хранения М_07. Принять как технический проход нельзя: по практике проектирования технический проход не уже 700 мм, меньше 600 мм — критично, а 280 мм — уже ширины плеч. Изменить границу частей либо состав М_07. Предложение исполнителя (27.10.2026): М_07 перенесена на торцевую стену А — 880 × 600 мм, штанга вдоль стены; проход по всей ширине гардеробной 880 мм, длина штанги 880 мм вместо 1700 — утвердить или выбрать иное.	Спорно Ждёт: решения	Дизайнер интерьера	проход через стык остаётся 280 мм: в часть гардеробной не пройти, пока не изменены граница частей или состав М_07	л. 12 — План размещения мебели и оборудования полный альбом
К-11	Высота потолка 2700 мм принята: на плане заказчика она не указана. От неё зависят вертикальные размеры альбома (развёртки, шкафы, плитка, объёмы работ). Замерить высоту на объекте.	Непонятно Ждёт: обмера	Архитектор-планировщик	Остаётся значение, принятое по исходным данным; оно не подтверждено, лист предварительный.	л. 5 — План планировки от заказчика
К-12	Две конструкции плана заказчика не определены: утолщение стены 190 × 1360 мм в гардеробной у спальни 2 (вентблок или пилон) и элемент 1470 × 160 мм на линии простенка кухни-гостиной (пилон, балка или барная стойка). Элемент 1470 × 160 мм на листах не показан, мебель от него свободна. Назначение определить на объекте.	Непонятно Ждёт: обследования	Архитектор-планировщик	Остаётся значение, принятое по исходным данным; оно не подтверждено, лист предварительный.	л. 5 — План планировки от заказчика л. 12 — План размещения мебели и оборудования

					Проект: Трёхкомнатная квартира
	Лист	№ док.	Подпись	Дата	Открытые вопросы, принятые допущения и конфликты. Лист 1 из 5
Дизайнер	Кырлан А.С.			04.11.26	

Стадия	Лист	Листов
П	77	92

Открытые вопросы и принятые допущения (продолжение)

№	Формулировка	Вид	Кто решает	Если решения нет	Лист, где это проявляется
К-13	Размеры сняты со скана плана заказчика по размерным цепочкам, контрольный обмер на объекте не выполнялся; толщины стен приняты 250 мм (наружные) и 150 мм (перегородки), на плане 85–190 мм. В двух местах принятое значение отличается от числа на плане: ширина гардеробной 1070 мм (на плане 1120 при перегородке 85 мм), ширина спальни 2 — 3130 мм (на плане 3120). Привязка стены прихожей к спальне 1 сдвинута на 40 мм относительно плана: на плане толщина стены 190 мм, в модели 150 мм (чистые размеры помещений — по плану, разница отнесена к толщинам стен). Подтвердить контрольным обмером.	Непонятно Ждёт: обмера	Архитектор-планировщик	Остаётся значение, принятое по исходным данным; оно не подтверждено, лист предварительный.	л. 5 — План планировки от заказчика
К-14	Разрешённая мощность 15 кВт принята по типовой квартире, технических условий в материалах объекта нет; расчётная мощность 11,8 кВт. Сверить с техническими условиями.	Непонятно Ждёт: документа	Инженер-электрик	Остаётся значение, принятое по исходным данным; оно не подтверждено, лист предварительный.	л. 34 — Однолинейная схема щита
К-15	Графы «Пров.» и «Н. контр.» в штампе пусты: их заполняет человек, подписи проверяющего и нормоконтролёра разработчик проекта не ставит; для выдачи нужны подписанты, отличные от разработчика. Решение автора (ИЗ-13): графы остаются пустыми, комплект предварительный.	Отсутствует Ждёт: решения	Нормоконтролёр	графы остаются пустыми; комплект предварительный, не проверен независимо	л. 3 — Список листов
К-16	Сдача разделов специалистами для этого проекта не оформлена (нет файлов решений по ролям). В альбоме нет листов «Пожарная безопасность» и «Звукоизоляция», программы испытаний и приёмки, допуска ГИПа. Решить, какие из этих разделов входят в состав работ; для входящих оформить сдачу.	Отсутствует Ждёт: решения	Главный инженер проекта (ГИП)	Исходных данных нет: на листе нет решения по этому пункту или оно условное; лист предварительный.	л. 3 — Список листов
К-17	Положение стояков условно, на объекте не замерено: стояки канализации и холодной воды — в коробе Ш1 248 × 459 в углу ванной и в стене-пилоне Ш2 270 мм между санузлом 2 и кухней (по плану заказчика). От положения стояков зависят привязки выводов воды и канализации, расстояния розеток до стояка (К-1) и места люков 300 × 400. Сверить положение стояков на объекте до разметки.	Непонятно Ждёт: обмера	Инженер ВК (вода, канализация)	Остаётся значение, принятое по исходным данным; оно не подтверждено, лист предварительный.	л. 17 — План выводов сантехники л. 18 — Схема разводки водопровода и канализации
К-18	Санузел 2: ниша 1600 × 1840 мм у входа закрыта перегородкой, ниша 660 × 260 мм (уступ по плану) — фальш-стеной с рамой инсталляции: проектное решение, на плане заказчика ниша у входа открыта в кухню-гостиную. От закрытия зависят размеры санузла 2 (1675 × 1580 мм), перегородка и фальш-стена в объёмах работ. Подтвердить закрытие ниш или оставить их открытыми.	Спорно Ждёт: решения	Архитектор-планировщик	Остаётся вариант, показанный на листе; он не утверждён, лист предварительный.	л. 17 — План выводов сантехники
К-19	Модель стиральной машины ОБ_01 не выбрана. Условие закупки (решение автора проекта, ИЗ-11): вертикальная загрузка, габарит в плане 400 × 600 мм (ширина 400 мм вдоль стены Б, глубина 600 мм), высота по паспорту (в расчёте 900 мм). Машина с фронтальной загрузкой или большего габарита проекту не подходит: перед люком ванна С_01, дверца не откроется. Тип загрузки и габарит до заказа сверить с паспортом выбранной модели, положение подводки — до закрытия трасс и разводки. В спецификации мебели и оборудования тот же габарит выведен по осям плана как 600 × 400 мм.	Отсутствует Ждёт: данных закупки, затем решения	Инженер ВК (вода, канализация)	машина не куплена: тип загрузки и габарит на листах условие закупки; купленная машина другого типа или габарита потребует пересмотра раскладки ванной	л. 17 — План выводов сантехники л. 26 — Спецификация сантехнического оборудования
К-20	Несущие стены не определены: проект дома и план БТИ в материалах объекта отсутствуют, тип и серия дома неизвестны, техническое заключение о несущих конструкциях не выполнялось. До заключения все существующие стены считаются несущими: демонтаж, новые проёмы и штробы в них не планируются. Нужно: запросить проект дома и поэтажный план БТИ, установить серию дома; несущие стены и допустимость вмешательства определяет техническое заключение специализированной организации.	Отсутствует Ждёт: документа, обследования	Архитектор-планировщик	Исходных данных нет: на листе нет решения по этому пункту или оно условное; лист предварительный.	полный альбом
К-21	Прямые углы помещений с кухней, санузлами, гардеробной и встроенной мебелью по скану не подтверждены: спальня 1, ванная, гардеробная, прихожая, кухня-гостиная, санузел 2. Нужен контрольный обмер: длины сторон и обе диагонали каждого помещения, отклонения углов от 90° у стен под встроенную мебель и плитку. Только после обмера в данных отмечаются прямые углы.	Отсутствует Ждёт: обмера	Архитектор-планировщик	углы принимаются прямыми по скану, не проверенными; встроенную мебель и плитку по размерам листов не заказывать до обмера	л. 5 — План планировки от заказчика л. 12 — План размещения мебели и оборудования
К-22	Состав подрядчиков и поставщиков (кто покупает и кто монтирует радиаторы, подоконники, двери, розетки) от заказчика не получен. Принята типовая схема частного ремонта (ИЗ-14): материалы и оборудование покупает заказчик по спецификациям проекта, монтаж ведёт подрядная бригада, приёмку скрытых работ ведёт автор. Схема уточняется договором подряда: нужен договор или состав подрядчиков и поставщиков от заказчика.	Отсутствует Ждёт: решения	Прораб-координатор	остаётся типовая схема: покупает заказчик, монтирует подрядная бригада, скрытые работы принимает автор; закрепление за конкретными подрядчиками не подтверждено	л. 3 — Список листов
К-23	Артикулы изделий отделки не выбраны. Инженерная доска (пом. 1, 3, 4, 6, 8), керамогранит пола (пом. 2, 5, 7), керамогранит стен (пом. 2, 7), керамогранит фартука кухни (пом. 6) и плинтус МДФ (пом. 1, 3, 4, 5, 6, 8) заданы характеристиками — «аналог по характеристикам», кода изделия производителя нет. Артикул выбирается при закупке: выбрать изделия, вписать артикулы в ведомость отделки и спецификации, цвет и тон принять по образцу из партии. Количество к заказу и упаковки — расчётные, по номинальным размерам, до выбора изделия. Калибр партии плитки для ванной и санузла 2 — отдельный вопрос К-2.	Отсутствует Ждёт: данных закупки, затем решения	Отделочник	материалы остаются описанными характеристиками; заказ по спецификации и подсчёт упаковок — только после выбора изделий	л. 43 — Раскладка плитки. Планы полов л. 44 — Раскладка плитки. Прихожая. Фартук кухни л. 27 — Раскладка плитки. Ванная. Развёртки стен л. 28 — Раскладка плитки. Санузел 2. Развёртки стен л. 42 — План покрытий пола л. С1, С2 — С1 Ведомость отделки помещений л. С3 — Спецификация отделочных материалов полный альбом
К-24	Модели встраиваемой техники кухни не выбраны: холодильник (М_19) и посудомоечная машина (М_21) заданы описанием «аналог по характеристикам» — без производителя, серии и кода. Размеры ниш и вентзазоры взяты по типовой схеме на 60 см, а не по паспорту модели: у разных изготовителей они расходятся, и модуль, сделанный по типовой нише, может не принять выбранную технику. Нужно: выбрать модели, получить монтажные схемы изготовителей и сверить ниши модулей, вентиляцию и подключение до заказа гарнитура. Вытяжка М_24 не встроена (подключение по паспорту изготовителя), но модель тоже не выбрана — выбирается вместе с остальной техникой. Проект кухни целиком — К-8.	Отсутствует Ждёт: данных закупки, затем решения	Мебельщик	ниши остаются по типовой схеме на 60 см, не подтверждённой паспортом модели; модули кухни не заказывать до выбора техники	л. Д_4 — Кухня (пом. 6). Развёртка гарнитура л. 8 — Кухня (пом. 6). Монтажная схема

					Проект: Трёхкомнатная квартира
	Лист	№ док.	Подпись	Дата	Открытые вопросы, принятые допущения и конфликты. Лист 2 из 5
Дизайнер	Кырлан А.С.			04.11.26	

Стадия	Лист	Листов
П	78	92

Открытые вопросы и принятые допущения (продолжение)

№	Формулировка	Вид	Кто решает	Если решения нет	Лист, где это проявляется
К-25	Скрытые двери Д-2 (спальня 1 и спальня 2), Д-3 (ванная) и Д-4 (гардеробная) заданы размером проёма 800×2100 со скана плана заказчика; проёмы существующие, расширять их до технического заключения (К-20) нельзя. Скрытый блок ставят в проём с зазором 10–15 мм на сторону, а коробка занимает часть ширины, поэтому полотно получается уже проёма; размеры короба и полотна задаёт изготовитель, модель не выбрана. У Д-3 и Д-4 принятая толщина стены 150 мм, по скану плана заказчика стена 85 мм: узел скрытой двери на листе узлов показан для принятой толщины 150 мм; по замеренной толщине его пересчитать. Порядок работ один: проём замеряют в чистоте после снятия отделки, короб ставят до штукатурки, полотно навешивают после чистовой отделки стен. Дверь Д-5 стоит в проектной перегородке П-1 (К-18): её проём 700 мм принят проектом, привязка к углу 50 мм; размер короба и полотна — по выбранной модели. Нужно: замерить проёмы и толщину стены в чистоте; решить, делать полотно под существующий проём (уже проёма) или расширять проём после технического заключения; выбрать модель блока и получить размеры короба.	Непонятно Ждёт: обмера, затем решения	Архитектор-планировщик	скрытые двери не заказывать (изготовление около 30 дней): размеры короба и полотна не определены, проёмы не расширять до технического заключения; узел показан для принятой толщины стены 150 мм	л. 29 — План размещения дверей л. 31, 32, С6, С7 — С6 Узлы
К-26	Входная дверь Д-1 существующая. По плану заказчика полотно открывается наружу, в общий коридор: на плане дверей и обмерном плане дуга показана наружу, как в данных объекта. Направление открывания на объекте не проверено и не выбирается за столом. Не решено, остаётся ли существующий блок или он заменяется: в ведомости объёмов работ заложена строка «Входная дверь, поставка с монтажом и откосами». Нужно: осмотр входной двери (сторона открывания, петли, коробка, откосы) и решение автора оставить блок или заменить, и с каким открыванием.	Непонятно Ждёт: обследования, затем решения	Архитектор-планировщик	на листах дверь показана как в данных объекта (открывание наружу, существующий проём); блок для заказа не определён	л. 29 — План размещения дверей
К-27	Окна ОК-1…ОК-4 в проекте существующие: демонтажа и замены окон нет ни на плане демонтажа, ни в ведомости объёмов работ; ведомость заполнения проёмов фиксирует их размеры, а не заказ новых блоков. Подоконная доска и глубина откоса не заданы: откосы считаются по умолчанию (толщина стены минус коробка 70 мм), подоконники в проекте не показаны; состояние окон и подоконников не обследовано. Нужно: осмотр окон и решение — окна и подоконники остаются существующими или заменяются.	Непонятно Ждёт: обмера, затем решения	Архитектор-планировщик	окна показаны существующими, заказ оконных блоков не предусмотрен; подоконники и глубина откосов приняты, не замерены	л. 29 — План размещения дверей
К-28	Сроки поставки и изготовления изделий с длинной поставкой не получены ни от одного поставщика: скрытые двери Д-2…Д-5, кухонный гарнитур, встраиваемая техника, керамогранит, инженерная доска, сантехника и инсталляции, встроенная мебель по замеру цеха. В данных нет срока (leadDays) ни у одной позиции. Типовые диапазоны практики — скрытые двери около 30 дней, кухня и корпусная мебель 4–8 недель от замера — это ориентир, а не срок поставщика: заказывать и назначать даты по ним нельзя. Нужно: запросить у поставщиков и изготовителей срок по выбранным моделям и записать его в данные позиции.	Отсутствует Ждёт: данных закупки, затем решения	Прораб-координатор	график закупок остаётся относительным: порядок и условия есть, дат заказа нет; заказ по типовым срокам не назначается	полный альбом
К-29	Климатический подрайон (СП 131.13330) не задан: принят не северный — жилые комнаты и кухня под потолком от 2,5 м (СП 54, п. 5.12); в IA, IБ, IГ, IД, IVA — от 2,7 м.	Отсутствует Ждёт: документа	Архитектор-планировщик	отметки потолков жилых — по 2,5 м; при северном подрайоне уровни ниже 2,7 м пересчитать до заказа каркаса	л. 30 — План потолков

Изменения проекта после выпуска листов (реестр изменений)

№	Дата	Лист	Было	Стало	Кто решил, подпись
ИЗ-1	05.10.2026	л. 17 — План выводов сантехники л. 35 — План розеток и электровыводов л. 26 — Спецификация сантехнического оборудования	В ванной и санузле 2 приборов отопления не было.	Добавлены электрические полотенцесушители IP44: С_04 в ванной (480 мм, низ 900 мм) и С_09 в санузле 2 (400 мм, низ 900 мм), выводы ЭВ6 и ЭВ7; мощность группы 13 — 2,4 кВт вместо 1,8 кВт. Основание: (в ванной и санузле есть полотенцесушитель — он же прибор отопления мокрой зоны); водяной не взят: стояка горячей воды в данных объекта нет, взят электрический IP44. Решение исполнителя: С_04, С_09, ЭВ6 и ЭВ7 остаются со знаком «**» (автором не подтверждены).	Утверждено: исполнитель по поручению Кырлана А.С., 05.10.2026. Предложил: исполнитель.
ИЗ-2	05.10.2026	л. 42 — План покрытий пола л. С1, С2 — С1 Ведомость отделки помещений	Ванная и санузел 2: пирог пола — стяжка 50 мм, слоя гидроизоляции в пироге не было.	Стяжка 33 мм и слой обмазочной гидроизоляции 2 мм (2 слоя, заведение на стены 200 мм); верх плиты — вровень с остальными помещениями. Основание: (в мокром помещении в пироге пола есть слой гидроизоляции с толщиной). Знак «**» у пола ванной и санузла 2 остаётся: решение исполнителя автором не подтверждено.	Утверждено: исполнитель по поручению Кырлана А.С., 05.10.2026. Предложил: исполнитель.
ИЗ-3	05.10.2026	л. 39 — Управление светильниками л. 38 — Техническое задание на подбор светильников	Кухня-гостиная: подвесы над столом (L14) и подсветка столешницы (L16) без светорегулятора, сценарии «Вечер» 50 % и «Ужин» 30 % недостижимы.	В выключателях S11 и S12 добавлены светорегуляторы (тип te); светильники Св42–Св44, лента подсветки и блок питания БП5 приняты диммируемыми. Основание: (промежуточный уровень сценария — только группе на светорегуляторе). Знак «**» у S11, S12, Св42–Св44 и БП5 остаётся.	Утверждено: исполнитель по поручению Кырлана А.С., 05.10.2026. Предложил: исполнитель.
ИЗ-4	05.10.2026	л. 35 — План розеток и электровыводов л. 72 — Развёртки стен А, Б, В. Санузел 2 (пом. 7)	Розетка Р33 (фен, санузел 2) на высоте 1200 мм, в перекрестье швов плитки.	Розетка Р33 на высоте 1100 мм, вне шва плитки. Затем высота снижена до 1000 мм вместе с Р7 и Р8 — запись ИЗ-9. Основание: (розетка — в центре плитки или на шве, не в перекрестье швов).	Утверждено: исполнитель по поручению Кырлана А.С., 05.10.2026. Предложил: исполнитель.
ИЗ-5	05.10.2026	полный альбом л. Д_4 — Кухня (пом. 6). Развёртка гарнитура	Кухня-гостиная: вывод «вытяжка» был, самой вытяжки в мебели не было; холодильник М_19 описан только нишей.	Добавлена вытяжка над варочной панелью М_24 (600 × 400 × 600 мм, низ 1600 мм); холодильник М_19 описан как встраиваемый 60 см с вентзазорами в цоколе и под карнизом. Основание: (под вывод «вытяжка» и «холодильник» в помещении должна стоять сама техника). Знак «**» у М_24 и М_19 остаётся; проект кухни заказчиком не утверждён (К-8).	Утверждено: исполнитель по поручению Кырлана А.С., 05.10.2026. Предложил: исполнитель.

					Проект: Трёхкомнатная квартира
	Лист	№ док.	Подпись	Дата	
Дизайнер	Кырлан А.С.			04.11.26	Открытые вопросы, принятые допущения и конфликты. Лист 3 из 5

Стадия	Лист	Листов
П	79	92

Изменения проекта после выпуска листов (реестр изменений) (продолжение)

№	Дата	Лист	Было	Стало	Кто решил, подпись
ИЗ-6	05.10.2026	л. 12 — План размещения мебели и оборудования л. 11 — Колерная карта	Марки: кухня К1…К14, шкафы П5 и П9, декор Д1…Д9.	Марки: мебель М (кухня ОБ_03, М_15, М_16, М_17, М_18, М_19, М_20, М_22, М_23, М_21, шкафы М_13 и М_14), декор ДК1…ДК9; у полотенцесушителя санузла 2 — С_09, потому что С_05 занят мойкой. Позиции не менялись. В поле lightCheck образцов «D65 и лампа проекта» заменено на «D65, лампа проекта» (смысл прежний: два источника сличения).	Не утверждено: подписи нет. решение исполнителя; на утверждение А. С. Кырлана
ИЗ-7	05.10.2026	полный альбом л. 9 — Шкафы. Монтажная схема	Шкаф-купе (П5, ныне М_13) 2600×600 мм: способ сборки не задан; диагональ боковины 2668 мм больше высоты до потолка 2620 мм.	Задана сборка стоя на месте (assembly: in-place): готовый корпус не поднять. Решение подтверждено автором 05.10.2026 (вопрос К-10 закрыт): размер корпуса не меняется, готовый корпус не поднять — сборка стоя на месте.	Утверждено: Кырлан А.С., автор проекта, 05.10.2026. Предложил: решение автора проекта, оформлено исполнителем по его поручению (запись внесена разработчиком по замечанию проверки).
ИЗ-8	05.10.2026	л. 35 — План розеток и электровыводов полный альбом	В ванной и санузле 2 не было вывода к вентилятору вытяжки и коробки уравнивания потенциалов.	Добавлены выводы к вентиляторам: ЭВ4 (ВР1, ванная) и ЭВ5 (ВР3, санузел 2) — группа 3, высота 2389 мм, включение с основным светом, таймер выбега в вентиляторе; и коробки уравнивания потенциалов КУП1 (ванная) и КУП2 (санузел 2) — высота 300 мм, у входа, вне зон 0–2, проводник от шины PE щита ЩК, сечение — по проекту ЭОМ. Основание: правила проверки (питание вентилятора вытяжки мокрого помещения) и (КУП в помещении с ванной или душем). Заказчик эти позиции не заказывал; решение исполнителя, ЭВ4, ЭВ5, КУП1 и КУП2 остаются со знаком «**» (автором поштучно не утверждены).	Утверждено: исполнитель по поручению Кырлана А.С., 05.10.2026. Предложил: исполнитель.
ИЗ-9	05.10.2026	л. 35 — План розеток и электровыводов полный альбом	Розетки Р7 (стиральная машина) и Р8 (фен) в ванной — 1200 мм, Р33 (фен, санузел 2) — 1100 мм, с флагом решения: высота не обоснована назначением.	Р7, Р8 и Р33 на высоте 1000 мм — верхний предел нормы (ПУЭ, п. 6.6.30, не выше 1 м); флаг решения снят. Назначение стиральной машины и фена не требует большей высоты. Р12, Р17, Р18, Р19 и Р25 остались выше 1 м по назначению (решение исполнителя; основание записано в самой позиции, вопрос К-7): Р12, Р18 и Р19 — 1100 мм, в одной зоне с выводами ТВ и LAN, которые тоже на 1100 мм; Р17 — 1700 мм, рядом с ЩС на высоте щита (1700 мм); Р25 — 2000 мм, над нишей М_19 за съёмной панелью с доступом, как и БП5. Высоты Р7, Р8, Р33 и всех перечисленных автором поштучно не подтверждены, знак «**» у них остаётся.	Утверждено: исполнитель по поручению Кырлана А.С., 05.10.2026. Предложил: исполнитель.
ИЗ-10	05.10.2026	л. 35 — План розеток и электровыводов полный альбом	Розетки Р7 (стиральная машина) и Р8 (фен) в ванной, Р33 (фен) в санузле 2 стояли в зоне 3 по ПУЭ, но ближе 2,5 м от границы зоны 1 по британской норме BS 7671 (п. 701.512.3); какая норма принята — вопрос К-6.	Принята норма ПУЭ (п. 7.1.48): розетки в зоне 3 помещения с ванной или душем допустимы при защите УЗО 30 мА. Положение розеток не менялось. Основание: розетки вне зон 0–2 (до границы зоны 1: Р7 — 650 мм, Р8 — 1220 мм, Р33 — 800 мм), исполнение IP44, группы 12 и 13 защищены УЗО 30 мА типа А. Это сознательное отступление от зарубежной нормы BS 7671: в России она не действует, по ней в таком месте допустима только бритвенная розетка с разделительным трансформатором. Высота розеток — отдельный вопрос К-7.	Утверждено: Кырлан А.С., автор проекта, 05.10.2026. Предложил: решение автора проекта, оформлено исполнителем по его поручению.
ИЗ-11	05.10.2026	л. 17 — План выводов сантехники л. 26 — Спецификация сантехнического оборудования л. 35 — План розеток и электровыводов л. 13–15 — Спецификация мебели и оборудования	Ванная: стиральная машина ОБ_01 фронтальной загрузки 600 × 600 мм, габарит условный (модель не выбрана); перед люком ванна С_01, свободно 50 мм вместо 500 — дверца не откроется (вопросы К-1, К-19).	Утверждена стиральная машина с вертикальной загрузкой, габарит в плане 400 × 600 мм (ширина 400 вдоль стены Б, глубина 600). На плане ОБ_01 уменьшена с 600 × 600 до 400 × 600, место у стены Б прежнее (500 мм от стены А), розетка Р7 остаётся на стене Б у машины. Габарит и тип загрузки — условие закупки, а не пожелание: машина с фронтальной загрузкой или большего габарита проекту не подходит (перед люком ванна С_01). Условие записано в спецификации сантехнического оборудования, на листе выводов сантехники и в вопросе К-19 (задание на закупку). Модель по-прежнему не выбрана: габарит и подводку сверить по паспорту до закрытия трасс. Спецификация мебели и оборудования выводит габарит машины по осям плана — 600 × 400 мм: это тот же размер (глубина 600 в комнату, ширина 400 вдоль стены).	Утверждено: Кырлан А.С., автор проекта, 05.10.2026. Предложил: решение автора проекта, оформлено исполнителем по его поручению.
ИЗ-12	05.10.2026	л. Д_4 — Кухня (пом. 6). Развёртка гарнитура л. 35 — План розеток и электровыводов л. 13–15 — Спецификация мебели и оборудования	Кухня-гостиная: раскладка гарнитура и выводы техники приняты по типовой расстановке, проект кухни не утверждён (вопрос К-8).	Раскладка гарнитура принята проектной: мойка М_20 у шахты Ш2, посудомоечная М_21 рядом с мойкой, варочная панель и духовой шкаф в М_22, вытяжка М_24, холодильник М_19. Условие: до начала черновых работ сверить раскладку и выводы техники с чертежом кухни от изготовителя; расхождения вносятся в реестр изменений, выводы пересматриваются по его чертежу. Проект кухни остаётся неутверждённым до этой сверки: позиции М_20 и М_22 сохраняют знак «*», примечание о выводах кухонной техники на листах сохранено, вопрос К-8 открыт.	Утверждено: Кырлан А.С., автор проекта, 05.10.2026. Предложил: решение автора проекта, оформлено исполнителем по его поручению.
ИЗ-13	05.10.2026	л. 3 — Список листов	Графы «Пров.» и «Н. контр.» основной надписи пусты (вопрос К-15); как с ними поступать — не записано.	Графы «Пров.» и «Н. контр.» остаются пустыми: независимой проверки и нормоконтроля проекта не было, автор проекта сам себе их не подписывает. Комплект выпускается предварительным: пока нет подписи проверяющего и нормоконтролёра, отличных от разработчика, он не считается окончательным.	Утверждено: Кырлан А.С., автор проекта, 05.10.2026. Предложил: решение автора проекта, оформлено исполнителем по его поручению.
ИЗ-14	05.10.2026	л. 3 — Список листов	Матрицы ответственности (делает / поставляет / принимает / хранит) нет; кто покупает и кто монтирует — не определено.	Принята типовая схема частного ремонта: материалы и оборудование покупает заказчик по спецификациям проекта; монтаж ведёт подрядная бригада; приёмку скрытых работ ведёт автор проекта; хранение — по договору подряда. Распределение закреплено по радиаторам, подоконникам, дверям и коробам скрытых дверей, розеткам и выключателям, сантехническим приборам, светильникам, отделочным материалам и плитке. Это схема по умолчанию, не факт: состав подрядчиков и поставщиков от заказчика не получен (вопрос К-22), схема уточняется договором подряда.	Не утверждено: подписи нет. решение исполнителя; на утверждение А. С. Кырлана

					Проект: Трёхкомнатная квартира
					Открытые вопросы, принятые допущения и конфликты. Лист 4 из 5
	Лист	№ док.	Подпись	Дата	
Дизайнер	Кырлан А.С.			04.11.26	

Стадия	Лист	Листов
П	80	92

Изменения проекта после выпуска листов (реестр изменений) (продолжение)


№	Дата	Лист	Было	Стало	Кто решил, подпись
ИЗ-15	05.10.2026	л. 35 — План розеток и электровыводов полный альбом	Розетка Р7 (стиральная машина, ванная) на стене Б со смещением 685 мм: 348 мм от стояка холодной воды Ст В1-1 при практике приёмки не ближе 500 мм.	Р7 на стене Б со смещением 985 мм (на 300 мм дальше вдоль стены, по-прежнему у стиральной машины ОБ_01; высота 1000 мм прежняя): до стояка Ст В1-1 644 мм. Новое место — на шве плитки. Расстояние Р7 до границы зоны 1 стало 691 мм вместо 650 мм, названных в ИЗ-10; принятая там норма ПУЭ и положение Р8 и Р33 не затронуты. Положение стояков условно (К-17): отступ сделан от принятого положения, не от замера. Решение исполнителя; знак «**» у Р7 остаётся (высота — вопрос К-7).	Не утверждено: подписи нет. решение исполнителя; на утверждение А. С. Кырлана
ИЗ-16	06.10.2026	л. 17 — План выводов сантехники л. 18 — Схема разводки водопровода и канализации л. 26 — Спецификация сантехнического оборудования л. 31, 32, С6, С7 — С6 Узлы	Короб стояков Ш1 в углу ванной: в данных 180 × 450 мм (х 7890), на листе узлов 248 × 459 мм. Стояк канализации Ø110 с изоляцией 20 мм и просветом 40 мм до стенки в 180 мм не помещается: размер не годился ни как внутренний, ни как наружный. Стиральная машина ОБ_01 стояла в 50 мм от короба (у 500).	Один источник габарита: внутренний 195 × 406 мм (трубы Ст К1-1 Ø110 и Ст В1-1 Ø32, изоляция 20 мм, просвет 40 мм, считая от стен угла), обшивка 53 мм (профиль 28 + ГКЛВ 2 × 12,5) на свободных сторонах, наружный габарит каркаса 248 × 459 мм; короб остаётся в углу у стен (х 7822, у 0). Облицовка плиткой — сверх наружного габарита. Стиральная машина ОБ_01 сдвинута на 10 мм (у 510) — зазор до короба 51 мм при требовании не менее 50 мм. Положение стояков по-прежнему условно (К-17), размер короба пересчитывается по замеру. Решение исполнителя; знак «*» у стояков Ст К1-1 и Ст В1-1 (от них — положение и размер короба, К-17) и у машины ОБ_01 остаётся: автор их поштучно не утверждал.	Не утверждено: подписи нет. решение исполнителя; на утверждение А. С. Кырлана
ИЗ-17	06.10.2026	л. 36 — План слаботочных сетей полный альбом	Состав и места слаботочки в данных проекта заданы проектировщиком: щит слаботочный ЩС, точки доступа Wi-Fi АР1 и АР2. План заказчика их не содержит, подтверждения заказчика в данных нет.	Слаботочка остаётся предложением проектировщика, заказчиком не утверждена: щит слаботочный ЩС в Прихожей (стена Г, 3350 мм от угла, высота 1700 мм, рядом со щитом ЩК; ввод оптики, ONT, роутер, патч-панель), точка доступа АР1 в Прихожей (потолок, х 6800, у 6300) и точка доступа АР2 в Кухне-гостиной (потолок, х 12000, у 5500), питание PoE, кабель U/UTP кат. 6. Основание: (если заданы слаботочные точки, задан и слаботочный щит, к которому они сходятся); число и места точек доступа — ориентир практики «одна на 40–60 м²». Заказчик состав и места слаботочки не задавал и не подтверждал: решение исполнителя, знак «**» у ЩС, АР1 и АР2 остаётся до утверждения автором; число и места точек доступа проверить по замеру уровня сигнала после монтажа.	Не утверждено: подписи нет. решение исполнителя; предложение проектировщика, на утверждение А. С. Кырлана
ИЗ-18	30.10.2026	л. Д_4 — Кухня (пом. 6). Развёртка гарнитура л. 8 — Кухня (пом. 6). Монтажная схема л. 64 — Развёртка стены В1. Кухня-гостиная (пом. 6), кухонный фронт л. 29 — План размещения дверей л. 17 — План выводов сантехники л. 12 — План размещения мебели и оборудования	Кухонный ряд М_19, М_20, М_22 3800 мм посажен от черновой грани стены Б при чистовой длине стены 3770; дверь Д-5 с простенком 50 мм до шахты Ш2; мойка С_05 500×450 против выреза 700×480; ТВ в спальне 2 только точками ЭОМ.	М_22 — 1775 (ряд 3775, зазор 10 мм до чистовой грани под компенсатор); Д-5 — offset 825 (простенок 150); С_05 — 700×480 по вырезу М_20; в спальне 2 добавлен ТВ ОБ_02 на кронштейне над комодом М_11. Знак «**» у Д-5 и ОБ_02 до подписи автора.	Не утверждено: подписи нет. решение исполнителя; предложение проектировщика, на утверждение А. С. Кырлана

Примечания


1. Номера листов — по ведомости рабочих чертежей комплекта (лист «Общие данные»).
2. Графа «Если решения нет» показывает состояние решения на листах; влияние на сроки и стоимость по пунктам не оценивалось.
3. Пункт, по которому принято решение, при следующем выпуске комплекта из таблиц исключается.

					Проект: Трёхкомнатная квартира	
	Лист	№ док.	Подпись	Дата	Открытые вопросы, принятые допущения и конфликты. Лист 5 из 5	Стадия / Лист / Листов
Дизайнер	Кырлан А.С.			04.11.26		П / 81 / 92


Вид с фасадами

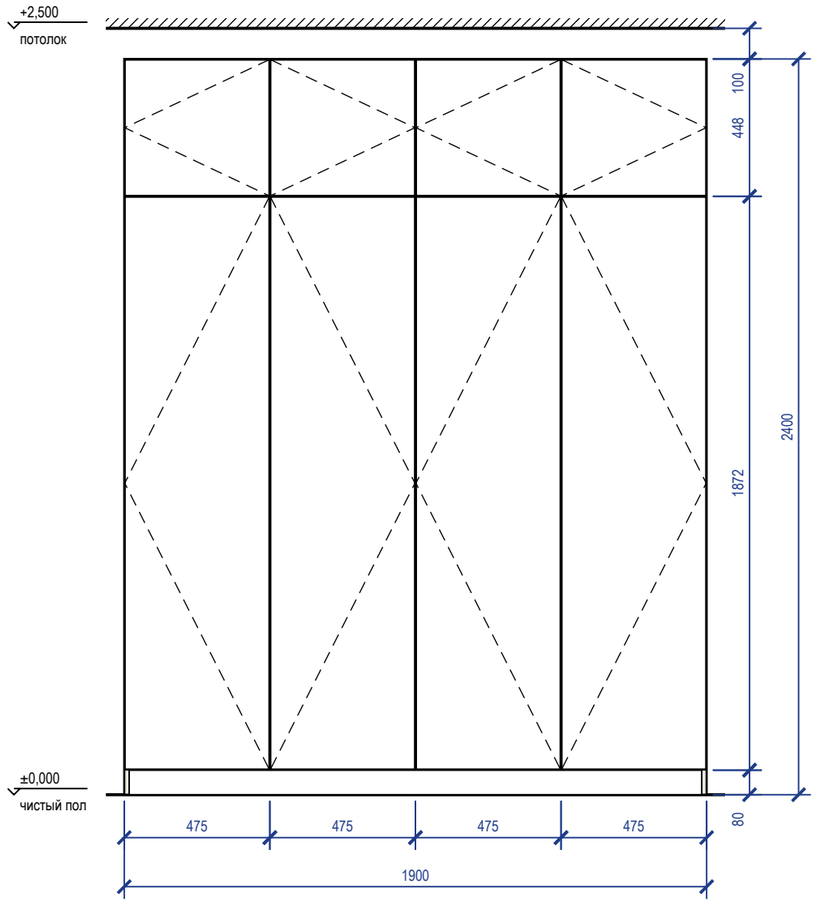


Вид без фасадов

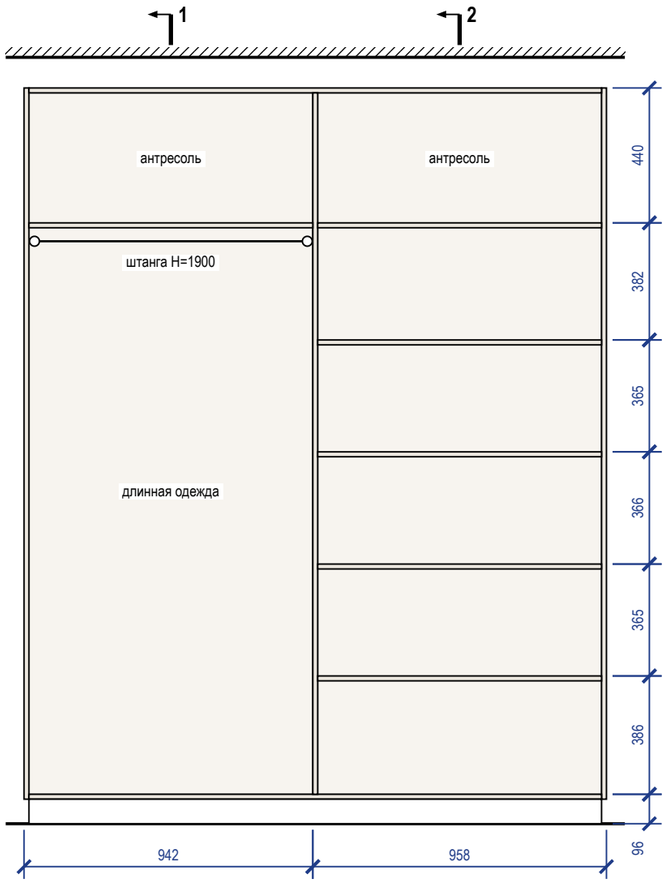

Разрез 1-1

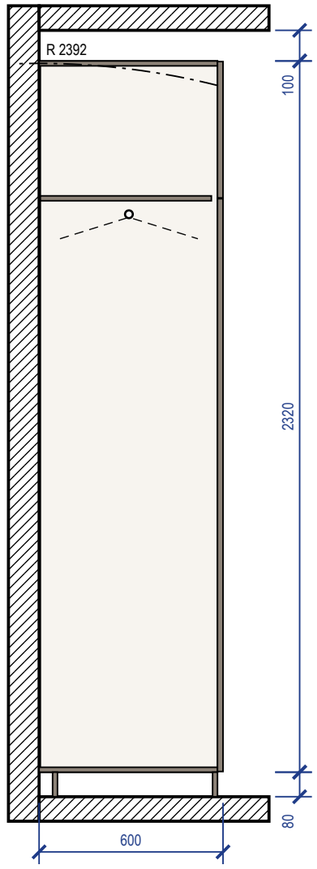


Разрез 2-2

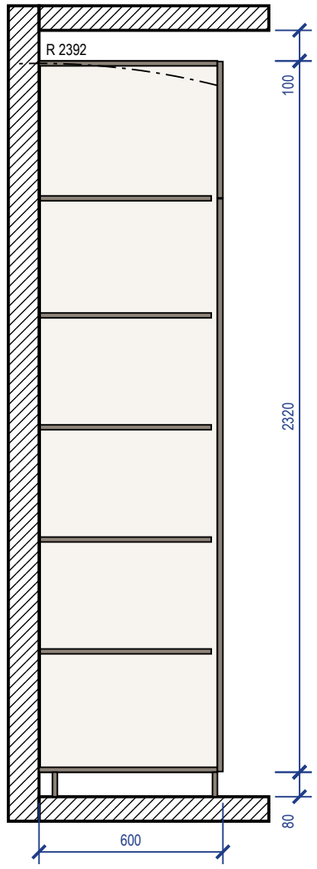

Примечания


1. Размеры — в мм по чистовой отделке; изделие 1900×600×2400 (Ш×Г×В). Перед раскроем — контрольный замер цеха после чистовой отделки стен, пола и потолка.
2. Корпус — ЛДСП 16 мм, задняя стенка ХДФ 4 мм в паз, цоколь 80 мм на регулируемых опорах; фасады накладные — МДФ 18 мм, эмаль матовая, 18 мм; цвет — по колерной карте; петли с доводчиком: фасад 1869 мм — 4 петли, фасад 445 мм — 2 петли.
3. Кромка: скрытые торцы 0,4 мм, видимые 2 мм (ПВХ/АБС).
4. Номинальные зазоры: между фасадами 3 мм, фасад — стена и фасад — потолок не менее 3 мм, фасад ящика — стойка 2 мм.
5. Присадка по 32-й системе — выполняет цех.
6. Зазор до потолка 100 мм — закрыть планкой в цвет корпуса при монтаже.
7. Подъём корпуса: диагональ боковины без цоколя $\sqrt{(2320^2 + 582^2)} = 2392$ мм < 2500 мм до потолка — корпус собирается лёжа, поднимается поворотом и ставится на цоколь.
8. Крепление к стене от опрокидывания: уголок к стене, 2 шт.; основание стены и шаг анкеров — монтажная схема шкафов.

3D орто

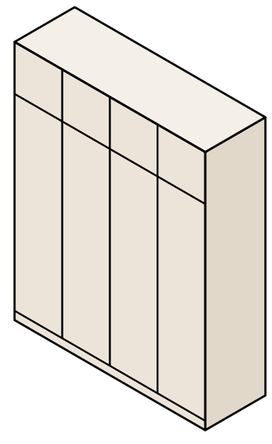


					Проект: Трёхкомнатная квартира	М 1:20
	Лист	№ док.	Подпись	Дата		
Дизайнер	Кырлан А.С.			04.11.26	Шкаф распашной М_05	Стадия: П; Лист: Д_1; Листов: 92


Общий вид

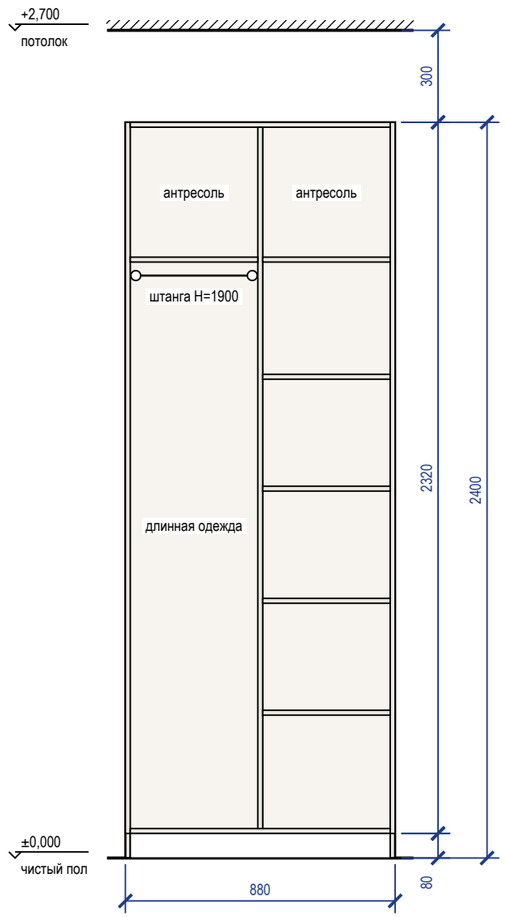


Наполнение, размеры в свету

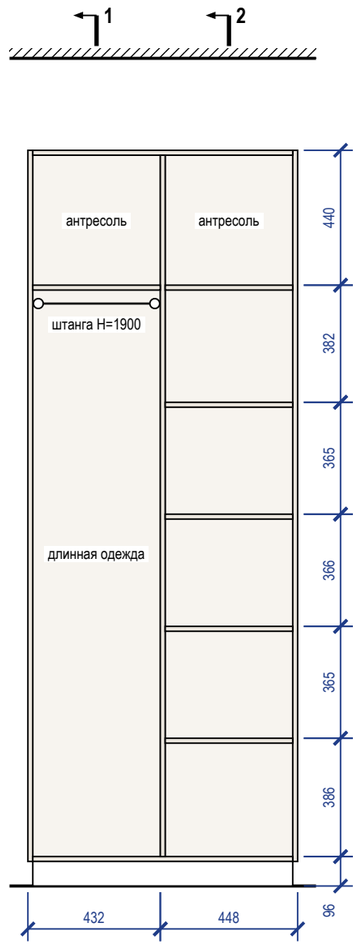

Разрез 1-1

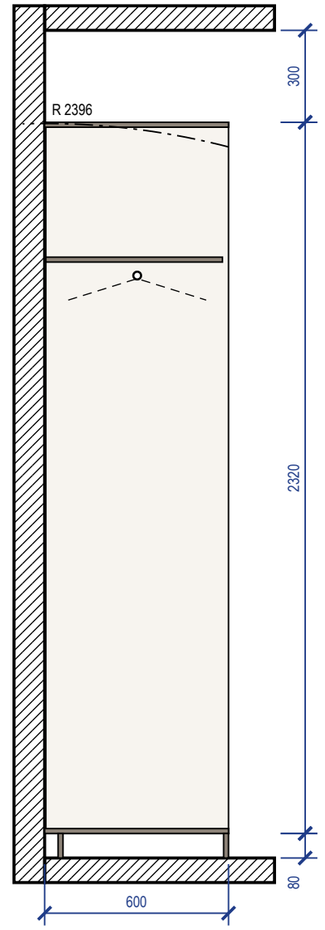


Разрез 2-2

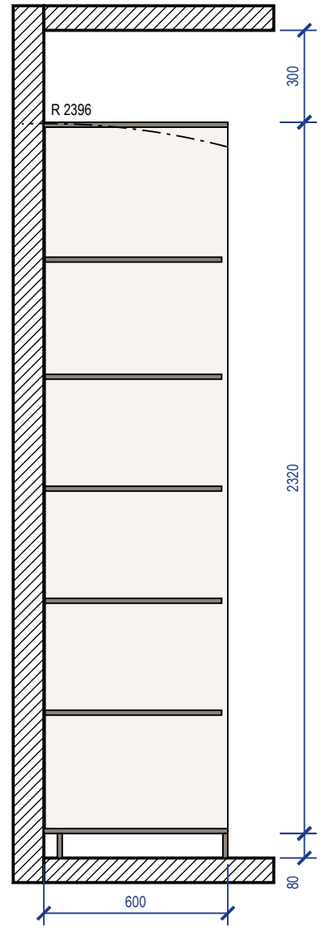

Примечания


1. Размеры — в мм по чистовой отделке; изделие 880×600×2400 (Ш×Г×В). Перед раскроем — контрольный замер цеха после чистовой отделки стен, пола и потолка.
2. Корпус — ЛДСП 16 мм, задняя стенка ХДФ 4 мм в паз, цоколь 80 мм на регулируемых опорах; открытая система: без фасадов.
3. Кромка: скрытые торцы 0,4 мм, видимые 2 мм (ПВХ/АБС).
4. Присадка по 32-й системе — выполняет цех.
5. Зазор до потолка 300 мм.
6. Подъём корпуса: диагональ боковины без цоколя √(2320² + 600²) = 2396 мм < 2700 мм до потолка — корпус собирается лёжа, поднимается поворотом и ставится на цоколь.
7. Крепление к стене от опрокидывания: крепление к стене, 3 точки; основание стены и шаг анкеров — монтажная схема шкафов.

3D орто

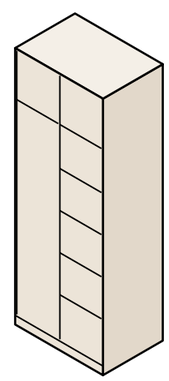


					Проект: Трёхкомнатная квартира	**М 1:20**
	Лист	№ док.	Подпись	Дата	Система хранения М_07	Стадия / Лист / Листов
Дизайнер	Кырлан А.С.			04.11.26		П / Д_2 / 92


Вид с фасадами

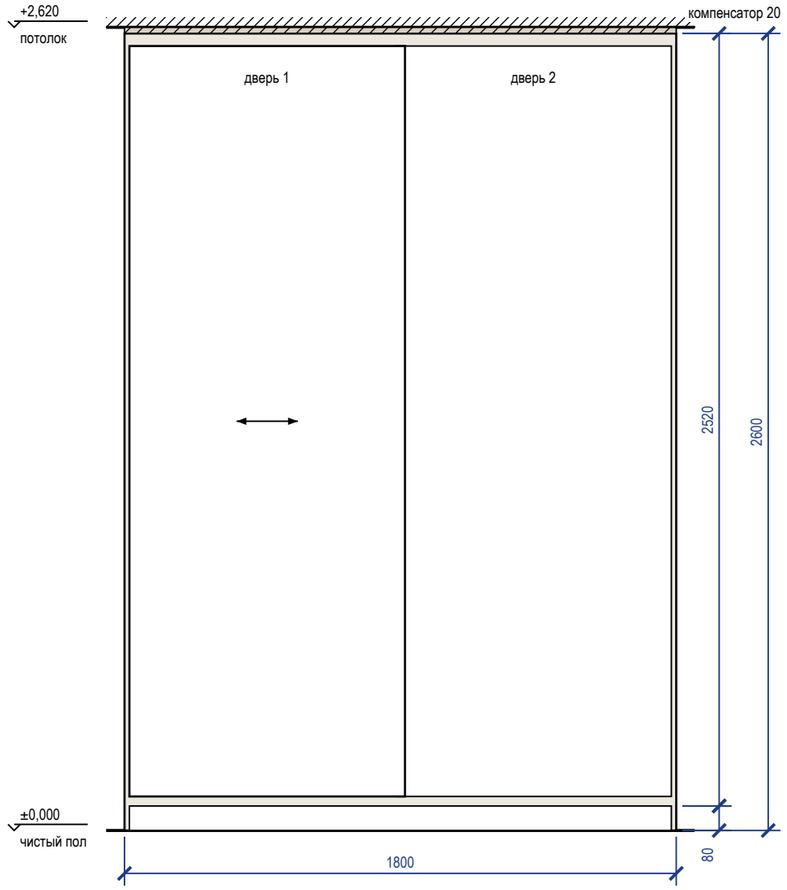


Вид без фасадов

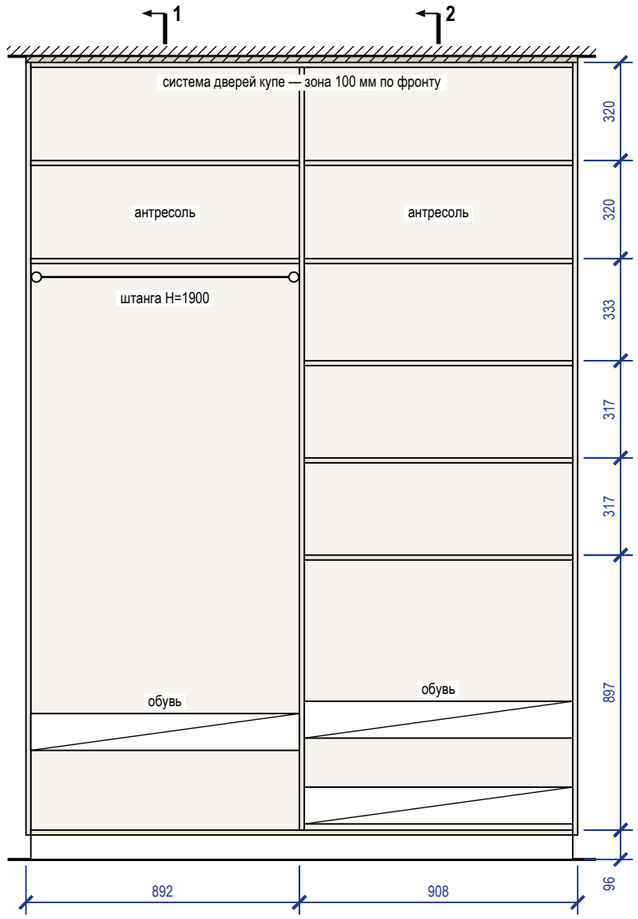

Разрез 1-1

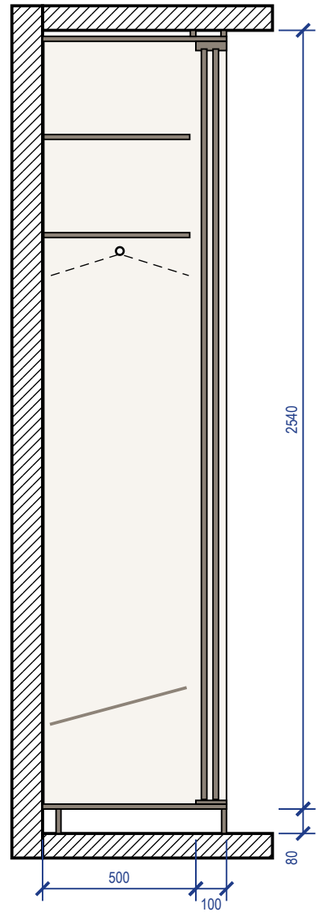


Разрез 2-2

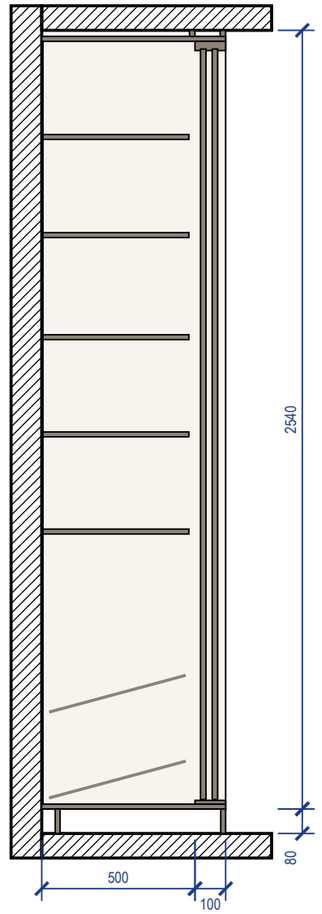

Примечания


1. Размеры — в мм по чистовой отделке; изделие 1800×600×2600 (Ш×Г×В). Перед раскроем — контрольный замер цеха после чистовой отделки стен, пола и потолка.
2. Корпус — ЛДСП 16 мм, задняя стенка ХДФ 4 мм в паз, цоколь 80 мм на регулируемых опорах; двери купе — ЛДСП 10 мм в алюминиевом профиле; нахлёст 30 мм, ширина двери 899 мм, высота — проём минус 40 мм; цвет — по колерной карте.
3. Кромка: скрытые торцы 0,4 мм, видимые 2 мм (ПВХ/АБС).
4. Номинальные зазоры: дверь купе — боковина 3 мм, фасад ящика — стойка 2 мм; ящики внутри купе — с накладкой 30 мм на стойке со стороны нахлёста дверей.
5. Присадка по 32-й системе — выполняет цех.
6. Компенсатор 20 мм — короб из ЛДСП по фронту и торцам, подгоняется к потолку при монтаже (припуск 20 мм), крепится к корпусу и к потолку.
7. Сборка стоя на месте (решение по изделию): корпус не собирается лёжа и не поднимается собранным — собирается в проектном положении у стены; траектория подъёма на виде не показана. Диагональ боковины без цоколя $\sqrt{(2520^2 + 600^2)} = 2590$ мм < 2620 мм до потолка.
8. Крепление к стене от опрокидывания — уголки 2 шт. к несущему основанию (монтажная схема шкафов).

3D орто

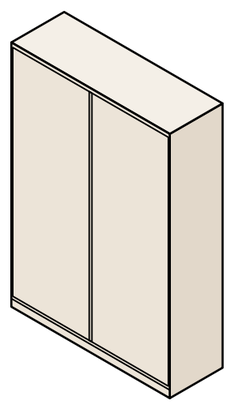


					Проект: Трёхкомнатная квартира	**М 1:20**
	Лист	№ док.	Подпись	Дата		
Дизайнер	Кырлан А.С.			04.11.26	Шкаф-купе М_13	Стадия: П; Лист: Д_3; Листов: 92


Вид с фасадами

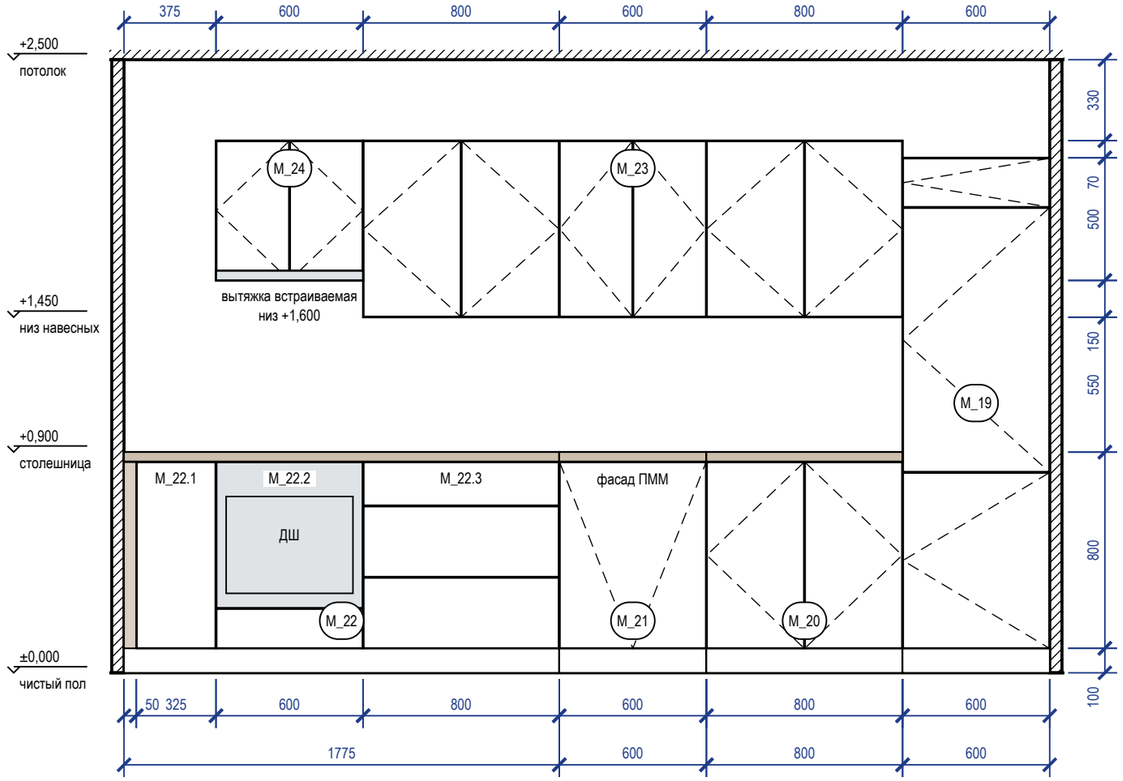


Вид без фасадов (наполнение, выводы)

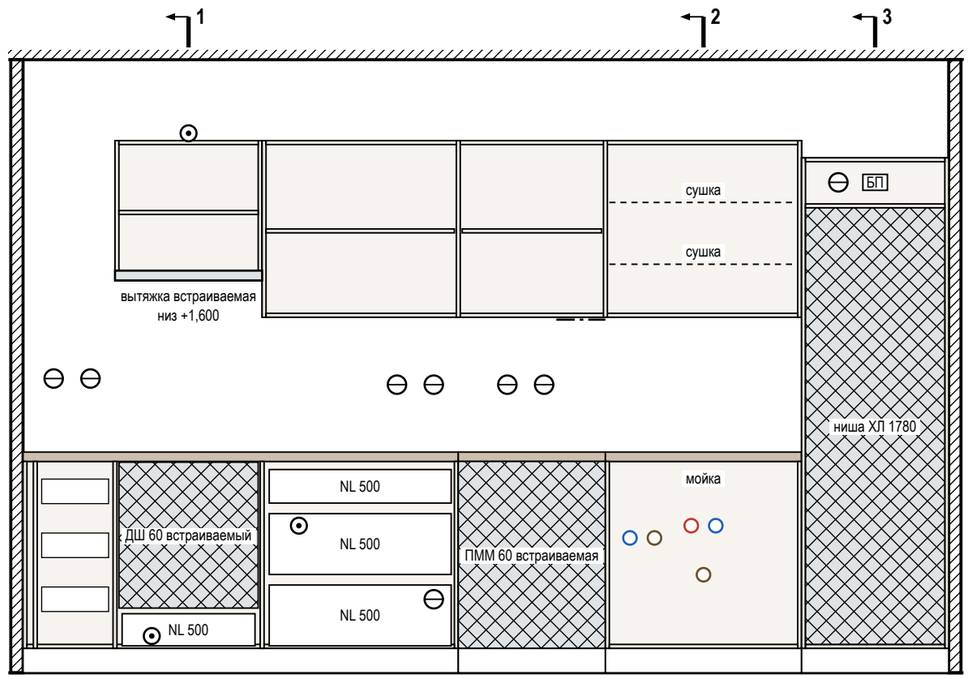


Разрез 1-1

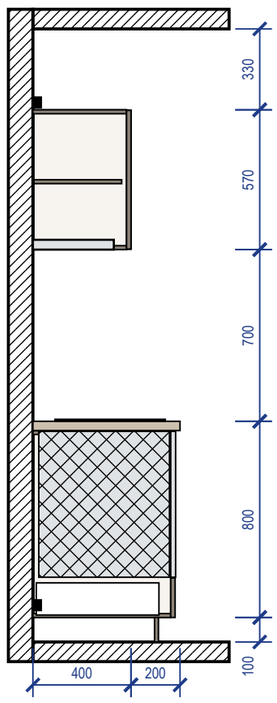


Разрез 2-2

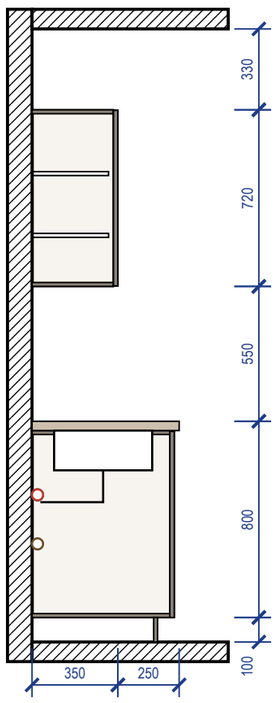

Разрез 3-3

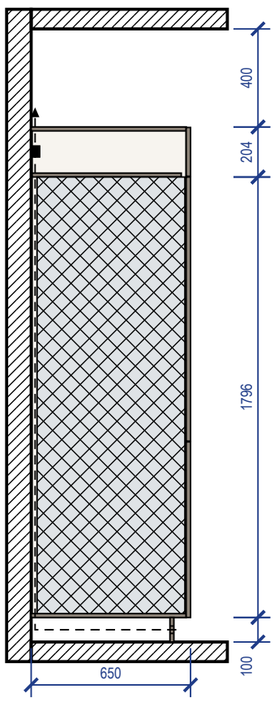

3D орто

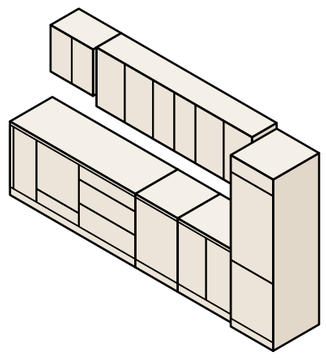

Примечания

1. Размеры — в мм по чистовой отделке, вид из помещения; марки — как на плане расстановки. Перед раскроем — контрольный замер цеха после фартука и пола.
2. Корпуса — ЛДСП 16 мм, задняя стенка ХДФ 4 мм; фасады — МДФ, эмаль матовая 18 мм, цвет по колерной карте; столешница 38 мм, свес 20 мм; цоколь 100 мм.
3. Кромка: скрытые торцы 0,4 мм, видимые 2 мм. Номинальные зазоры: между фасадами 3 мм, фасад — столешница 3 мм, фасад — стена не менее 3 мм.
4. Ящики полного выдвижения и петли — с доводчиком; присадка по 32-й системе — выполняет цех.
5. Вытяжка встраивается в дно навесного модуля M_24 над варочной: её низ на 1600 мм от пола, 700 мм над панелью (не меньше 650 мм).
6. Ниши техники (холодильник — ориентир 1780 мм) — по монтажным схемам выбранных моделей: решётка в цоколе и канал за пеналом холодильника, зазор за духовым шкафом, фасад ПММ на двери машины.

					Проект: Трёхкомнатная квартира	**М 1:25**
	Лист	№ док.	Подпись	Дата		
Дизайнер	Кырлан А.С.			04.11.26	Кухня (пом. 6). Развёртка гарнитура	

Стадия	Лист	Листов
П	Д_4	92

Ведомость отделки помещений (форма 1 прил. А ГОСТ 21.501-2018). Лист 1 из 2

№	Наименование помещения	Потолок			Стены и перегородки			Низ стен (плинтус)			Пол		Примечание
		Вид отделки	Код цвета	S, м²	Вид отделки	Код цвета	S, м²	Вид отделки	Код цвета	L, м	Вид отделки	S, м²	
1	Спальня 1 17,75 м²	ГКЛ по каркасу П113, отм. +2,500; +2,600; окраска, Tikkurila Anti-Reflex 2, глубокоматовая, 2 слоя, подготовка Q3	Tikkurila V503	17,75	Окраска, Farrow & Ball Modern Emulsion, матовая, 2 слоя, подготовка Q3 Акцент — стена А: окраска, Farrow & Ball Modern Emulsion, матовая, 2 слоя, подготовка Q3	Farrow & Ball No. 241 Farrow & Ball No. 30	25,00 14,18	Плинтус МДФ h=80 мм, аналог: МДФ под покраску 80×16	Farrow & Ball No. 241	16,8	Аналог: инженерная доска, дуб натуральный, масло, 1-полосная, 14/4 мм, на клею; тип 1, отм. ЧП ±0,000	17,75	Н стен 2500 (до потолка); плинтус в цвет: стены
2	Ванная 4,43 м²	ГКЛВ по каркасу П113, отм. +2,389; окраска, Tikkurila Luja 7, матовая, 2 слоя, подготовка Q3	Tikkurila V503	4,43	Облицовка плиткой, аналог: керамогранит под травертин, матовый, 600×1200×9 мм, клей C2 TE S1, затирка CG2WA	по артикулу	18,61	нет			Аналог: керамогранит ректифицированный под травертин, матовый, 600×600×9 мм; тип 2, отм. ЧП −0,015	4,43	Н стен 2404 (до потолка); гидроизоляция обмазочная, 2 слоя, с заведением на стены 200 мм; над ванной — до 2000 и 300 мм за борт (по пирогу пола); тест проливом и акт скрытых работ
3	Гардеробная 1,85 м²	Существующий потолок, отм. +2,700; окраска, Tikkurila Anti-Reflex 2, глубокоматовая, 2 слоя, подготовка Q3	Tikkurila V503	1,85	Окраска, Tikkurila Harmony, матовая, 2 слоя, подготовка Q3	Tikkurila V503	14,74	Плинтус МДФ h=80 мм, аналог: МДФ под покраску 80×16	Tikkurila V503	5,3	Аналог: инженерная доска, дуб натуральный, масло, 1-полосная, 14/4 мм, на клею; тип 1, отм. ЧП ±0,000	1,85	Н стен 2700 (до потолка); плинтус в цвет: стены
4	Спальня 2 12,80 м²	ГКЛ по каркасу П113, отм. +2,500; +2,600; окраска, Tikkurila Anti-Reflex 2, глубокоматовая, 2 слоя, подготовка Q3	Tikkurila V503	12,80	Окраска, Farrow & Ball Modern Emulsion, матовая, 2 слоя, подготовка Q3 Акцент — стена А: окраска, Farrow & Ball Modern Emulsion, матовая, 2 слоя, подготовка Q3	Farrow & Ball No. 241 Farrow & Ball No. 30	22,21 10,22	Плинтус МДФ h=80 мм, аналог: МДФ под покраску 80×16	Farrow & Ball No. 241	13,6	Аналог: инженерная доска, дуб натуральный, масло, 1-полосная, 14/4 мм, на клею; тип 1, отм. ЧП ±0,000	12,80	Н стен 2500 (до потолка); плинтус в цвет: стены
5	Прихожая 7,13 м²	ГКЛ по каркасу П113, отм. +2,620; окраска, Tikkurila Anti-Reflex 2, глубокоматовая, 2 слоя, подготовка Q3	Tikkurila V503	7,13	Окраска, Farrow & Ball Modern Emulsion, матовая, 2 слоя, подготовка Q3	Farrow & Ball No. 241	21,86	Плинтус МДФ h=80 мм, аналог: МДФ под покраску 80×16	Farrow & Ball No. 241	7,8	Аналог: керамогранит ректифицированный под травертин, матовый, 600×1200×9 мм; тип 3, отм. ЧП ±0,000	7,13	Н стен 2620 (до потолка); матовая моющаяся, класс 1 EN 13300 — осознанно вместо полуматовой; плинтус в цвет: стены
6	Кухня-гостиная 29,20 м²	ГКЛ по каркасу П113, отм. +2,500; +2,600; окраска, Tikkurila Anti-Reflex 2, глубокоматовая, 2 слоя, подготовка Q3	Tikkurila V503	29,20	Окраска, Farrow & Ball Modern Emulsion, матовая, 2 слоя, подготовка Q3 Акцент — стена А: окраска, Farrow & Ball Modern Emulsion, матовая, 2 слоя, подготовка Q3 Фартук кухни (стена В): облицовка керамогранитом, аналог: керамогранит под травертин, матовый, 1200×600×9 мм, клей C2 TE S1, затирка CG2WA	Farrow & Ball No. 241 Farrow & Ball No. 30 по артикулу	35,53 14,18 1,85	Плинтус МДФ h=80 мм, аналог: МДФ под покраску 80×16	Farrow & Ball No. 241	22,2	Аналог: инженерная доска, дуб натуральный, масло, 1-полосная, 14/4 мм, на клею; тип 1, отм. ЧП ±0,000	29,20	Н стен 2500 (до потолка); матовая моющаяся, класс 1 EN 13300 — осознанно вместо полуматовой; плинтус в цвет: стены
7	Санузел 2 2,29 м²	ГКЛВ по каркасу П113, отм. +2,389; окраска, Tikkurila Luja 7, матовая, 2 слоя, подготовка Q3	Tikkurila V503	2,29	Облицовка плиткой, аналог: керамогранит под травертин, матовый, 600×1200×9 мм, клей C2 TE S1, затирка CG2WA	по артикулу	13,10	нет			Аналог: керамогранит ректифицированный под травертин, матовый, 600×600×9 мм; тип 2, отм. ЧП −0,015	2,29	Н стен 2404 (до потолка); гидроизоляция обмазочная, 2 слоя, с заведением на стены 200 мм; у душа — до 2000 и 500 мм за поддон (по пирогу пола); тест проливом и акт скрытых работ
8	Коридор 3,50 м²	ГКЛ по каркасу П113, отм. +2,620; окраска, Tikkurila Anti-Reflex 2, глубокоматовая, 2 слоя, подготовка Q3	Tikkurila V503	3,50	Окраска, Farrow & Ball Modern Emulsion, матовая, 2 слоя, подготовка Q3	Farrow & Ball No. 241	14,17	Плинтус МДФ h=80 мм, аналог: МДФ под покраску 80×16	Farrow & Ball No. 241	4,5	Аналог: инженерная доска, дуб натуральный, масло, 1-полосная, 14/4 мм, на клею; тип 1, отм. ЧП ±0,000	3,50	Н стен 2620 (до потолка); матовая моющаяся, класс 1 EN 13300 — осознанно вместо полуматовой; плинтус в цвет: стены

Примечания

1. Ведомость продолжена на листе 2 из 2; итоги, сводка площадей и примечания — на последнем листе ведомости.

					Проект: Трёхкомнатная квартира
	Лист	№ док.	Подпись	Дата	Ведомость отделки помещений. Лист 1 из 2
Дизайнер	Кырлан А.С.			04.11.26	

Стадия	Лист	Листов
П	С1	92

Ведомость отделки помещений (форма 1 прил. А ГОСТ 21.501-2018). Лист 2 из 2

№	Наименование помещения	Потолок			Стены и перегородки			Низ стен (плинтус)			Пол		Примечание
		Вид отделки	Код цвета	S, м²	Вид отделки	Код цвета	S, м²	Вид отделки	Код цвета	L, м	Вид отделки	S, м²	
	Итого			**78,95**			**205,64**			**70,3**		**78,95**	

Сводка площадей по материалам отделки

Поверхность	Материал / код цвета	Серия	Площадь, м²
Потолок	Tikkurila V503	Anti-Reflex 2	72,23
Потолок	Tikkurila V503	Luja 7	6,72
Стены	Farrow & Ball No. 241	Modern Emulsion	118,77
Стены	Farrow & Ball No. 30	Modern Emulsion	38,58
Стены	облицовка плиткой 600×1200×9 мм	аналог: керамогранит под травертин, матовый	31,71
Стены	Tikkurila V503	Harmony	14,74
Фартук	облицовка керамогранитом 1200×600×9 мм	аналог: керамогранит под травертин, матовый	1,85

Примечания

1. Площади поверхностей — по чистым граням стен до отделки: стены = периметр × высоту от чистого пола помещения до низа потолка минус проёмы (облицовка плиткой — до верха облицовки); плинтус = периметр минус дверные проёмы; пол и потолок — по площади помещения. Количество плиток по раскладке. Площади помещений — с учётом всех частей помещения; откосы в площадь стен не входят.
2. Акцентные стены и фартук — отдельными строками, их площадь вычтена из основной отделки стен помещения; фартук — над нижними модулями кухни от столешницы до низа навесных шкафов, где шкафов нет — на 600 мм.
3. Плинтус — длина по периметру за вычетом дверных проёмов; примыкания к наличникам и встроенной мебели — по развёрткам.
4. Формат плитки — Ш×В×Т (ширина × высота в положении укладки × толщина), мм; на полу — вдоль стен А/В × вдоль стен Б/Г.
5. Коды цвета — по веерам производителей; колеровка каждой краски одной партией, проверка выкраса при свете D65 и при лампах проекта.
6. Уровни подготовки Q1–Q4 — система Knauf, не норма ГОСТ/СП; допуски поверхностей — по СП 71.13330.2017 (действующая редакция).
7. «аналог:» — изделие задано характеристиками, марку и артикул согласовать с заказчиком до закупки.

					Проект: Трёхкомнатная квартира
	Лист	№ док.	Подпись	Дата	Ведомость отделки помещений. Лист 2 из 2
Дизайнер	Кырлан А.С.			04.11.26	

Стадия	Лист	Листов
П	С2	92

Поз.	Наименование и техническая характеристика	Тип, марка, обозначение документа	Код продукции	Поставщик	Ед. изм.	Кол.	Образец	Примечание
	Лакокрасочные материалы							
1	Краска интерьерная водно-дисперсионная акриловая для стен, матовая, класс мокрого истирания 1 по EN 13300, база A; цвет по вееру Farrow & Ball No. 241 «Skimming Stone», колеровка машинная	Farrow & Ball Modern Emulsion		Farrow & Ball	л	32,5		поз. К1 колерной карты; пом. 1, 4, 5, 6, 8; S = 118,8 м² × 2 сл. × 0,12 л/м² = 28,5 л, +10 % и 0,5 л на подкраску → ≥ 31,9 л; тара 6 × 5 л + 1 × 2,5 л
2	Краска интерьерная водно-дисперсионная акриловая для акцентных стен, матовая, класс мокрого истирания 1 по EN 13300, база C; цвет по вееру Farrow & Ball No. 30 «Hague Blue», колеровка машинная	Farrow & Ball Modern Emulsion		Farrow & Ball	л	12,5		поз. К2 колерной карты; пом. 1, 4, 6; S = 38,6 м² × 2 сл. × 0,12 л/м² = 9,3 л, +10 % и 0,5 л на подкраску → ≥ 10,7 л; тара 2 × 5 л + 1 × 2,5 л
3	Краска интерьерная водно-дисперсионная акриловая для потолков, глубокоматовая, класс мокрого истирания 2 по EN 13300, база A; цвет по вееру Tikkurila V503 «Winter», колеровка машинная	Tikkurila Anti-Reflex 2		Tikkurila	л	19,8		поз. К3 колерной карты; пом. 1, 3, 4, 5, 6, 8; S = 72,2 м² × 2 сл. × 0,12 л/м² = 17,3 л, +10 % и 0,5 л на подкраску → ≥ 19,6 л; тара 2 × 9 л + 2 × 0,9 л
4	Краска интерьерная водно-дисперсионная акриловая для потолков, матовая, класс мокрого истирания 1 по EN 13300, база A; цвет по вееру Tikkurila V503 «Winter», колеровка машинная	Tikkurila Luja 7		Tikkurila	л	2,7		поз. К5 колерной карты; пом. 2, 7; S = 6,7 м² × 2 сл. × 0,12 л/м² = 1,6 л, +10 % и 0,5 л на подкраску → ≥ 2,3 л; тара 1 × 2,7 л
5	Краска интерьерная водно-дисперсионная акриловая для стен, матовая, класс мокрого истирания 1 по EN 13300, база A; цвет по вееру Tikkurila V503 «Winter», колеровка машинная	Tikkurila Harmony		Tikkurila	л	4,5		поз. К6 колерной карты; пом. 3; S = 14,7 м² × 2 сл. × 0,12 л/м² = 3,5 л, +10 % и 0,5 л на подкраску → ≥ 4,4 л; тара 1 × 2,7 л + 2 × 0,9 л
6	Краска для МДФ и дерева в цвет Farrow & Ball No. 241 «Skimming Stone» — окраска плинтуса; блеск не ниже блеска стен	марка не задана			л	1,7		поз. К4; пом. 1, 4, 5, 6, 8; L = 65,1 м, S = 6,2 м² × 2 сл. × 0,12 л/м² + 10 %; продукт подобрать в веере Farrow & Ball
7	Краска для МДФ и дерева в цвет Tikkurila V503 «Winter» — окраска плинтуса; блеск не ниже блеска стен	марка не задана			л	0,5		поз. К7; пом. 3; L = 5,3 м, S = 0,5 м² × 2 сл. × 0,12 л/м² + 10 %; продукт подобрать в веере Tikkurila
8	Грунтовка акриловая под окраску стен и потолков — из системы производителя краски	по системе краски			м²	252		площадь окраски стен, акцентов и потолков; 1 слой перед окраской; расход — по ТУ грунтовки
	Плитка и керамогранит							
9	Керамогранит под травертин, 600×600×9 мм, ректификат, водопоглощение 0,1 % (BIa), противоскольжение R10, PEI IV	аналог по характеристикам			м²	9,72		шов 2 мм; Ванная, пол; Санузел 2, пол; по раскладке 24 шт (S = 6,72 м²), с запасом 27 шт
10	Керамогранит под травертин, 600×1200×9 мм, ректификат, водопоглощение 0,1 %	аналог по характеристикам			м²	56,88		шов 2 мм; Ванная, стены А–Г; Ванная, короб стояков Ш1 248×459; Ванная, короб инсталляции; Санузел 2, стены А–Г; Санузел 2, короб инсталляции; по раскладке 67 шт (S = 33,26 м²), с запасом 79 шт
11	Керамогранит ректифицированный под травертин, матовый, 600×1200×9 мм, водопоглощение 0,1 % (BIa), противоскольжение R10, PEI IV	аналог по характеристикам			м²	10,08		шов 2 мм; Прихожая, пол; по раскладке 12 шт (S = 7,13 м²), с запасом 14 шт
12	Керамогранит под травертин, матовый, 1200×600×9 мм, ректификат, водопоглощение 0,1 % (BIa)	аналог по характеристикам			м²	3,60		шов 2 мм; Кухня-гостиная, фартук (ст. В); по раскладке 4 шт (S = 1,85 м²), с запасом 5 шт
	Напольные покрытия							
13	Инженерная доска, дуб натуральный, масло, 1-полосная, 14/4 мм, эмиссия E1, укладка на клей	аналог по характеристикам			м²	69,7		пом. 1, 3, 4, 6, 8; S = 65,10 м² + 7 % (прямая укладка); к заказу — кратно упаковке
14	Клей для паркета и инженерной доски, эластичный (СМП / полиуретановый)	по рекомендации производителя доски			м²	66		площадь приклейки; расход и шпатель — по ТУ клея
	Погонажные изделия							
15	Плинтус МДФ под покраску 80×16, крепление к стене, окраска в цвет Farrow & Ball No. 241	аналог по характеристикам			м	72		пом. 1, 4, 5, 6, 8; L = 65,1 м (периметр без дверных проёмов) + 10 % на подрезку; в штуках — по длине планки
16	Плинтус МДФ под покраску 80×16, крепление к стене, окраска в цвет Tikkurila V503	аналог по характеристикам			м	6		пом. 3; L = 5,3 м (периметр без дверных проёмов) + 10 % на подрезку; в штуках — по длине планки
	Смеси и материалы для облицовки							
17	Затирка для швов плитки, класс CG2WA по EN 13888	Mapei Ultracolor Plus 132		Mapei	кг	3,8		по раскладке (a+b)/(a·b) × шов × t × 1,6 + 10 %; в т. ч. 0,7 кг — позиции раскладки без марки
18	Клей плиточный C2 TE S1 по EN 12004, слой 5 мм	Ceresit CM 17		Ceresit	кг	384		16 меш. по 25 кг; 1,5 кг/м² на 1 мм слоя + 10 %; в т. ч. 73 кг — позиции раскладки без марки
19	Гидроизоляция обмазочная мокрых зон: пол, стены по периметру, зоны замачивания; 2 слоя с армирующей лентой в углах	аналог по характеристикам			м²	20		площадь по листу раскладки плитки + 10 %; расход смеси — по ТУ
20	Лента демпферная по периметру пола из плитки	аналог по характеристикам			м	22,4		периметр без дверных проёмов + 10 %

Примечания

1. Количества — из геометрии проекта: площади поверхностей по чистым граням стен до отделки (те же, что в ведомости отделки и колерной карте), плитка, клей и затирка — по раскладке плиточника; в графе «Кол.» — к заказу, с запасом.
2. Краска: расход 0,12 л/м² на слой в 2 слоя, если по ТУ не задан иной; запас 10 % и 0,5 л на подкраску каждого кода. Один код — одна партия, колеровка машинная в колеровочном центре бренда; в заказ — только после утверждения выкраса (колерная карта). Фасовка — по каталогу бренда на дату выпуска; к заказу — не меньше расчётного объёма.
3. «Аналог по характеристикам» — допускается изделие другого производителя с характеристиками не ниже указанных, по согласованию с автором проекта.
4. Графы «Код продукции» и «Масса 1 ед.» не заполнены: коды по классификатору продукции не присвоены, масса единицы до 25 кг (ГОСТ 21.110-2013).
5. Грунтовка и клей для доски указаны площадью обработки; объём — по ТУ выбранного продукта.

					Проект: Трёхкомнатная квартира
	Лист	№ док.	Подпись	Дата	
Дизайнер	Кырлан А.С.			04.11.26	Спецификация отделочных материалов
					Стадия: П; Лист: С3; Листов: 92

Список покупок: материалы для магазина

№	Что купить	Артикул или характеристика	Нужно с запасом	Брать в магазине	Фасовка	Уточнить в магазине	Помещения	Кто покупает
Покрытия полов и облицовка								
1	Инженерная доска (дуб натуральный, рабочий слой 4 мм, эмиссия E1, прямая укладка)	по характеристике: инженерная доска, дуб натуральный, масло, 1-полосная, 14/4 мм	70,38 м²	70,4 м²		уточнить в магазине: м² в упаковке	1, 3, 4, 6, 8	по проекту
2	Клей для паркетной и инженерной доски (эластичный, по ТУ изготовителя доски)	на выбор бригады по проекту	65,78 м²			уточнить в магазине: расход и фасовку — по выбранному продукту		бригада
3	Керамогранит 600×600 мм под травертин	по характеристике: керамогранит под травертин	27 шт	27 шт		уточнить в магазине: штук в коробке	2, 7	по проекту
4	Керамогранит 600×1200 мм под травертин	по характеристике: керамогранит под травертин	74 шт	79 шт		уточнить в магазине: штук в коробке	2, 7	по проекту
5	Керамогранит 600×1200 мм ректифицированный под травертин, матовый	по характеристике: керамогранит ректифицированный под травертин, матовый	14 шт	14 шт		уточнить в магазине: штук в коробке	5	по проекту
6	Керамогранит 1200×600 мм под травертин, матовый	по характеристике: керамогранит под травертин, матовый	5 шт	5 шт		уточнить в магазине: штук в коробке	6	по проекту
Сухие смеси и гидроизоляция								
7	Клей плиточный цементный класса C2 TE S1 (ГОСТ Р 56387-2018)	Ceresit CM 17 или аналог	383,36 кг	16 меш.	мешок 25 кг			по проекту
8	Затирка цементная класса CG2WA, цвет — по колерной карте	Mapei Ultracolor Plus 132 или аналог	3,82 кг	2 упак.	упак. 2 кг			по проекту
9	Гидроизоляция обмазочная полимерная, 2 слоя, лента в углах, манжеты на выводах	на выбор бригады по проекту	19,97 м²			уточнить в магазине: расход и фасовку — по выбранному продукту	2, 7	бригада
10	Лента демпферная по периметру пола из плитки	на выбор бригады по проекту	22,4 м	23 м		уточнить в магазине: фасовку		бригада
11	Смесь цементно-песчаная для стяжки М200 (50 мм, 33 мм)	на выбор бригады по проекту	4,08 м³			уточнить в магазине: расход и фасовку — по выбранному продукту		бригада
12	Смесь штукатурная гипсовая для машинного и ручного нанесения по маякам, слой до 10 мм	на выбор бригады по проекту	218,21 м²			уточнить в магазине: расход и фасовку — по выбранному продукту	1, 2, 3, 4, 5, 6, 7, 8	бригада
Короба из ГКЛВ								
13	Лист ГКЛВ 12,5 мм, 2500 × 1200 мм, обшивка коробов в 2 слоя	на выбор бригады по проекту	10,85 м²	4 лист.	лист 3,00 м²		2, 7	бригада
14	Профиль стальной оцинкованный 27 × 28 мм: каркас коробов (стойки и направляющие)	на выбор бригады по проекту	26,65 м	9 шт	хлыст 3 м			бригада
Перегородки и облицовки из ГКЛВ								
15	Лист ГКЛВ 12,5 мм, 2500 × 1200 мм: обшивка перегородок и облицовок, 2 слоя на сторону	на выбор бригады по проекту	16,02 м²	6 лист.	лист 3,00 м²			бригада
16	Профиль направляющий ПН 100: по потолку и полу, перемычки над проёмами	на выбор бригады по проекту	3,52 м	2 шт	хлыст 3 м			бригада
17	Профиль стоечный ПС 100: стойки через шаг каркаса и короткие над проёмами	на выбор бригады по проекту	10,23 м	4 шт	хлыст 3 м			бригада
18	Профиль усиленный УА 100 (2,0 мм): стойки по краям проёма на полную высоту	на выбор бригады по проекту	5,94 м	2 шт	хлыст 3 м			бригада
19	Плита минераловатная звукопоглощающая в полость каркаса, толщина по глубине профиля 100 мм	на выбор бригады по проекту	3,14 м²			уточнить в магазине: расход и фасовку — по выбранному продукту		бригада
20	Лента уплотнительная самоклеящаяся под профили по потолку, полу и у примыканий к стенам	на выбор бригады по проекту	8,69 м	9 м		уточнить в магазине: фасовку		бригада
21	Саморезы для ГКЛ по металлу (по слоям обшивки), дюбели для направляющих — по ТУ изготовителя системы	на выбор бригады по проекту	14,56 м²			уточнить в магазине: расход и фасовку — по выбранному продукту		бригада

					Проект: Трёхкомнатная квартира	
	Лист	№ док.	Подпись	Дата		
Дизайнер	Кырлан А.С.			04.11.26	Список покупок	Стадия: П; Лист: С4; Листов: 92

Список покупок: материалы для магазина (продолжение)

№	Что купить	Артикул или характеристика	Нужно с запасом	Брать в магазине	Фасовка	Уточнить в магазине	Помещения	Кто покупает
22	Шпаклёвка для швов и мест креплений ГКЛВ под плитку (Q1)	на выбор бригады по проекту	4,87 м²			уточнить в магазине: расход и фасовку — по выбранному продукту		бригада
Слаботочные сети								
23	Кабель домофона — тип по системе поставщика	на выбор бригады по проекту	2,9 м	3 м		уточнить в магазине: длину бухты		бригада
24	Кабель коаксиальный RG-6 (75 Ом) к розеткам ТВ	на выбор бригады по проекту	29,1 м	30 м		уточнить в магазине: длину бухты		бригада
25	Кабель U/UTP кат. 6 (LAN, Wi-Fi и камеры по PoE)	на выбор бригады по проекту	61,2 м	62 м		уточнить в магазине: длину бухты		бригада
26	Гофротруба Ø20 для слаботочных линий, отдельно от силовых	на выбор бригады по проекту	83,9 м	84 м		уточнить в магазине: длину бухты		бригада
27	Розетка компьютерная RJ45, кат. 6, с рамкой и подрозетником	на выбор бригады по проекту	3 шт	3 шт	шт			бригада
28	Розетка телевизионная (коаксиальная) с рамкой и подрозетником	на выбор бригады по проекту	2 шт	2 шт	шт			бригада
29	Трубка или монитор домофона (поставка домофонной организации)	на выбор бригады по проекту	1 шт	1 шт	шт			по проекту
30	Щит слаботочный ЩС: корпус, DIN-рейка, розетки 220 В	на выбор бригады по проекту	1 шт	1 шт	шт			бригада
31	Патч-панель, портов не менее 5	на выбор бригады по проекту	1 шт	1 шт	шт			бригада
Лакокрасочные материалы								
32	Краска интерьерная акриловая, матовая, класс истирания 1	Farrow & Ball Modern Emulsion No. 30 «Hague Blue»	10,19 л	5 банк.	банка 2,5 л		1, 4, 6	по проекту
33	Краска интерьерная акриловая, матовая, класс истирания 1	Farrow & Ball Modern Emulsion No. 241 «Skimming Stone»	31,36 л	13 банк.	банка 2,5 л		1, 4, 5, 6, 8	по проекту
34	Краска интерьерная акриловая, глубокоматовая, класс истирания 2	Tikkurila Anti-Reflex 2 V503 «Winter»	19,07 л	8 банк.	банка 2,7 л		1, 3, 4, 5, 6, 8	по проекту
35	Краска интерьерная акриловая, матовая, класс истирания 1	Tikkurila Luja 7 V503 «Winter»	1,77 л	1 банк.	банка 2,7 л		2, 7	по проекту
36	Краска интерьерная акриловая, матовая, класс истирания 1	Tikkurila Harmony V503 «Winter»	3,89 л	2 банк.	банка 2,7 л		3	по проекту
37	Шпаклёвка финишная полимерная под окраску (стены и потолки, Q3)	на выбор бригады по проекту	276,14 м²			уточнить в магазине: расход и фасовку — по выбранному продукту		бригада
38	Грунтовка акриловая глубокого проникновения, 2 слоя	на выбор бригады по проекту	313,06 м²			уточнить в магазине: расход и фасовку — по выбранному продукту		бригада
Погонажные изделия и потолки								
39	Плинтус напольный МДФ под покраску, h=80 мм, крепление к стене	по характеристике: плинтус МДФ под покраску 80×16	77,37 м.п.	33 шт	хлыст 2,4 м		1, 3, 4, 5, 6, 8	по проекту
40	Потолок подвесной ГКЛ/ГКЛВ по каркасу Knauf П113: листы, профили, подвесы, лента, шпаклёвка швов	Knauf П113	77,1 м²			уточнить в магазине: расход и фасовку — по выбранному продукту		по проекту

Примечания


1. «Нужно с запасом» — расход по чертежам и раскладке плюс запас на подрезку и подкраску; «Брать в магазине» — то же количество в единицах, которыми продают (банки, мешки, упаковки, листы, штуки, литры).
2. «Уточнить в магазине» — фасовки этого товара в проекте нет: спросите у продавца, сколько в упаковке, и возьмите целое число упаковок не меньше «Нужно с запасом».
3. Плитку, доску и краску одного цвета берите одной партией (один калибр и тон на помещение) и сохраните чек и номер партии до конца ремонта.
4. «По характеристике» — артикул не выбран: подойдёт любой товар с этими свойствами, согласуйте его с дизайнером до покупки. «Бригада» материал выбирает и закупает бригада по своей технологии.
5. Помещения: 1 — Спальня 1; 2 — Ванная; 3 — Гардеробная; 4 — Спальня 2; 5 — Прихожая; 6 — Кухня-гостиная; 7 — Санузел 2; 8 — Коридор; «—» материал для нескольких помещений, расход по месту.

					Проект: Трёхкомнатная квартира
	Лист	№ док.	Подпись	Дата	Список покупок (окончание)
Дизайнер	Кырлан А.С.			04.11.26	

Стадия	Лист	Листов
П	С5	92


1 Порог 15 мм: мокрая зона — смежное помещение (М 1:5)

Применение: двери Д-5, Д-3

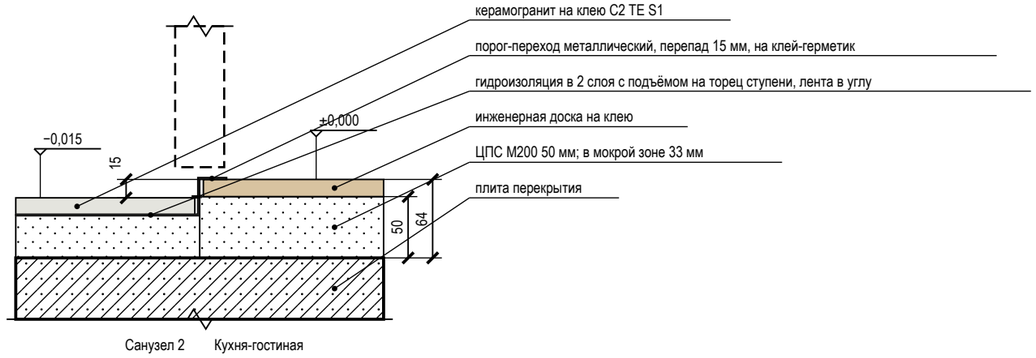


2 Стык покрытий пола Т-профилем без перепада (М 1:5)

Применение: проёмы 5↔6, 8↔5

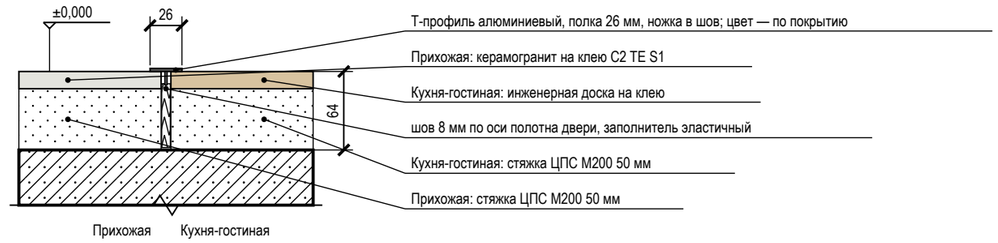


3 Дверь скрытого монтажа в плоскости стены, плинтус (М 1:5)

Применение: двери Д-2, Д-5, Д-3, Д-4

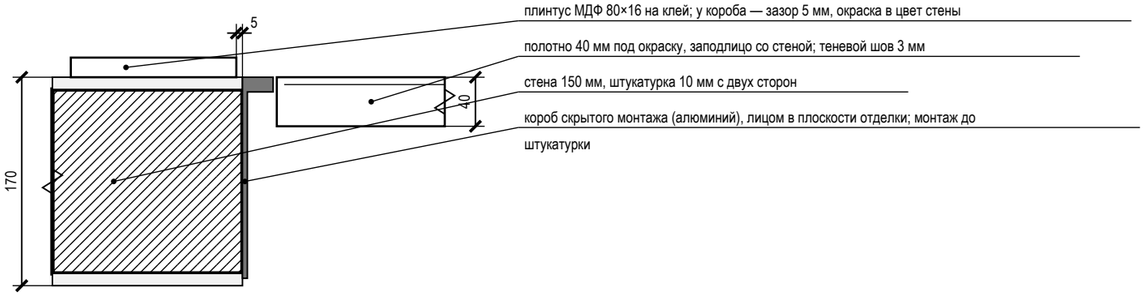

4 Короб стояков К1-1, В1-1 с люком и звукоизоляцией (М 1:10)

Применение: пом. 2

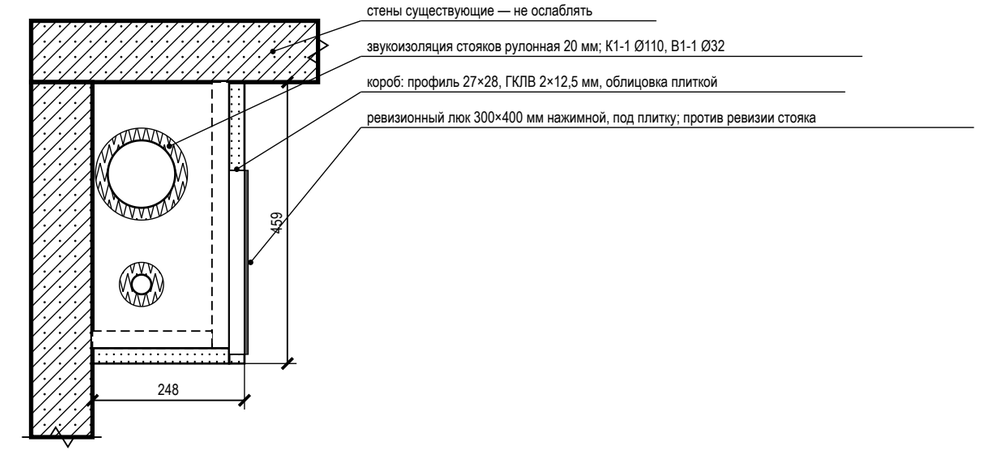

Условные обозначения

- железобетон (плита, стены) — условно: конструкция не установлена
- кладка, перегородка — условно: конструкция не установлена
- стяжка, раствор
- гипсокартон ГКЛВ
- звукоизоляция, эластичный заполнитель
- плитка, керамогранит на клею
- инженерная доска (покрытие пола)
- металлический профиль (порог, Т-профиль, короб двери)
- гидроизоляция (обмазочная, лента)

Примечания


1. Узлы — типовые решения проекта для мест, отмеченных выносками на листе схемы расположения развёрток и узлов; размеры — в мм, отметки — в м от ±0,000.
2. Узлы с гидроизоляцией, закладными и коробами скрытого монтажа принимаются по актам скрытых работ до закрытия отделкой; гидроизоляция — после теста проливом (24 ч).
3. Марки изделий (порог, Т-профиль, короб скрытой двери, люк) — по спецификациям; замена — на аналог с теми же габаритами по согласованию с автором проекта.
4. Материал плиты перекрытия и стен в узлах показан условно (железобетон, кладка): конструкция дома не установлена — крепёж, анкеры и толщины слоёв уточняются после обследования (до него — по допущениям общих указаний).
5. Узлы комплекта выпущены на 2 листах, нумерация узлов сквозная: 1–4 — лист С6 альбома (данный лист); 5–7 — лист С7 альбома.

					Проект: Трёхкомнатная квартира
	Лист	№ док.	Подпись	Дата	
Дизайнер	Кырлан А.С.			04.11.26	Узлы. Лист 1 из 2

Стадия	Лист	Листов
П	С6	92


5 Гидроизоляция санузла: заход на стены 200 мм, примыкание ванны (М 1:10)

Применение: пом. 2, 7

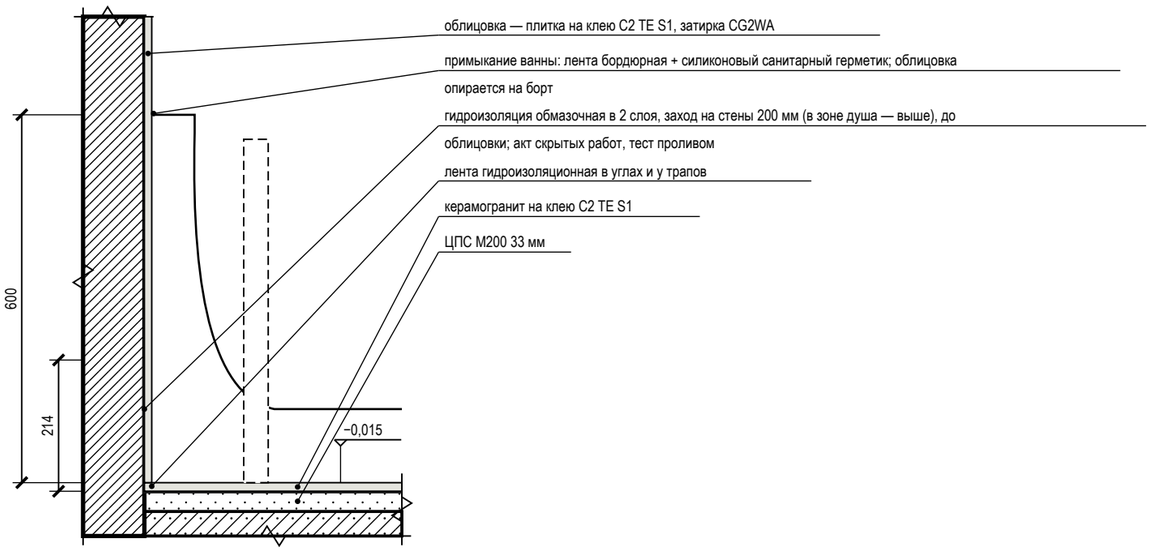


6 Плинтус МДФ 80×16 мм у окрашенной стены по доске (ламинату) (М 1:5)

Применение: пом. 1, 3, 4, 6, 8

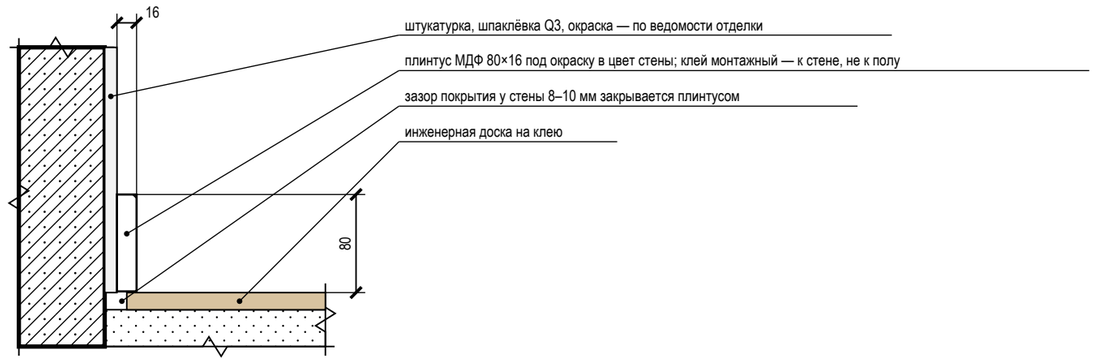

7 Плинтус МДФ 80×16 мм у окрашенной стены по керамограниту (плитке) (М 1:5)

Применение: пом. 5

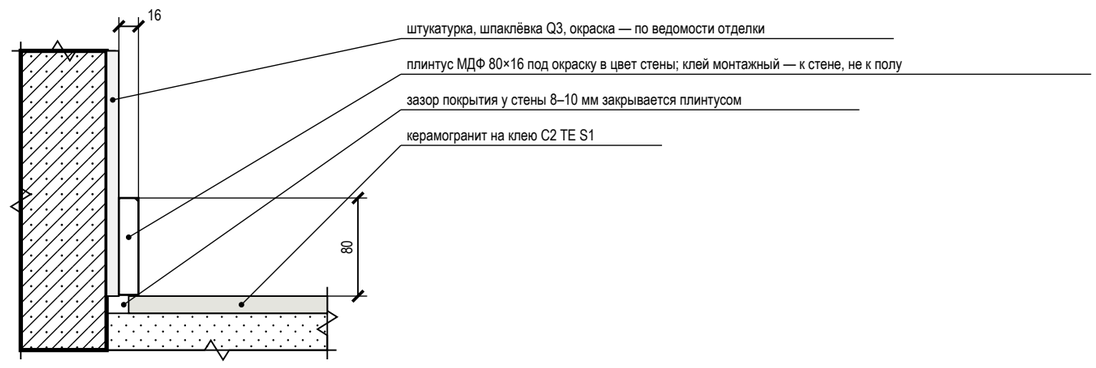

Условные обозначения

- железобетон (плита, стены) — условно: конструкция не установлена
- кладка, перегородка — условно: конструкция не установлена
- стяжка, раствор
- плитка, керамогранит на клею
- инженерная доска (покрытие пола)
- гидроизоляция (обмазочная, лента)

Примечания

1. Узлы — типовые решения проекта для мест, отмеченных выносками на листе схемы расположения развёрток и узлов; размеры — в мм, отметки — в м от ±0,000.
2. Узлы с гидроизоляцией, закладными и коробами скрытого монтажа принимаются по актам скрытых работ до закрытия отделкой; гидроизоляция — после теста проливом (24 ч).
3. Марки изделий (порог, Т-профиль, короб скрытой двери, люк) — по спецификациям; замена — на аналог с теми же габаритами по согласованию с автором проекта.
4. Материал плиты перекрытия и стен в узлах показан условно (железобетон, кладка): конструкция дома не установлена — крепёж, анкеры и толщины слоёв уточняются после обследования (до него — по допущениям общих указаний).
5. Узлы комплекта выпущены на 2 листах, нумерация узлов сквозная: 1–4 — лист С6 альбома; 5–7 — лист С7 альбома (данный лист).

					Проект: Трёхкомнатная квартира
	Лист	№ док.	Подпись	Дата	
Дизайнер	Кырлан А.С.			04.11.26	Узлы. Лист 2 из 2

Стадия	Лист	Листов
П	С7	92

выпуск 04.11.2026 № 503a52061a · стр. 92 из 92