L

LINEA

ДИЗАЙН-ПРОЕКТ ИНТЕРЬЕРА

Квартира 65 м²

Скандинавский

ПАЛИТРА ОТДЕЛКИ

NCS S 1502-Y50	NCS S 1002-Y50	V503	F&B No. 241	NCS S 0502-Y
31 %	22 %	20 %	12 %	8 %

АВТОР ПРОЕКТА

Кырлан Александр Сергеевич

Ноябрь 2026



План расстановки мебели · М 1:100

ОБЩАЯ ПЛОЩАДЬ	ПОМЕЩЕНИЙ	СТАДИЯ	ШИФР	ОСНОВА
65,24 м²	9, из них жилых 3	Проект · предварительно	ГД-2026-007-АИ	план заказчика, без обмера

Как оставить правку: кнопка «Правка к этому листу» в правом верхнем углу любого листа · все листы проекта: дизайн-студия-квартир.рф/review.html?p=gost-kv65

выпуск 04.11.2026 № 84932ed378 · стр. 1 из 83

Объект

Квартира 65 м²: 65 м², помещений 9, из них жилых 3.

Стиль: скандинавский 100 %. Стадия: предварительный альбом без обмера, планировка по плану заказчика.

Открытых вопросов 11, конфликтов разделов 0; изменений утверждено 0, ждут подписи 1.

Розетки и выводы

24 розетки (рамок 21), 3 вывода кабеля под технику и свет, 5 групп щита — всё с высотами от чистого пола: листы 32, 33.

Что решено (подписано вами)

Подписанных решений пока нет.

Что ждёт вашего ответа

К-1 — Размеры квартиры сняты с растрового плана заказчика без размерных цепочек: масштаб восстановлен по подписанным площадям помещений.

К-2 — Высота потолка на плане заказчика не указана, принята 2700 мм.

К-3 — Спальня (пом. 2) по плану заказчика без окна: жилая комната должна иметь естественное освещение (СП 54.13330.2022).

К-4 — Разрешённая мощность квартиры по ТУ неизвестна, принята 15 кВт.

К-5 — Кухня-гостиная (пом. 3): диван M_07 2200 × 950 стоит в полосе 1400 мм между спальней и кухней единственном проходе от двери из коридора в комнату.

К-6 — Спальня (пом. 2) без окна: приток не решён — бризер на внутренней стене Б не работает (нужно отверстие в наружной стене), а наружная стена А занята изголовьем кровати…

К-7 — Вентканалы на плане заказчика не показаны: ВК-1 и ВК-2 приняты проектировщиком у кухни, ванная (пом. 7) от них далеко — вытяжка ВР3 идёт воздуховодом ≈ 4 м через санузел.

К-8 — Проём санузла (пом. 6, марка Д-5) по плану заказчика 550×2100 — уже ряда стандартных полотен (600–900): полотно ≈ 450 под заказ, проход меньше 600.

К-9 — Климатический подрайон (СП 131.13330) не задан: принят не северный — жилые комнаты и кухня под потолком от 2,5 м (СП 54, п. 5.12).

К-10 — Несущие стены не определены: плана БТИ, проекта дома и технического заключения в материалах объекта нет .

К-12 — Циркуляция ГВС в данных не задана — циркуляционного трубопровода на схеме нет.

Предложено, ждёт подписи

ИЗ-1 — Диван M_07 у стены А основной части (x 250…2450, y 1650…2600), стол M_05 перед ним (x 1100…2100, y 2800…3800), кресло M_06 у окна 2 (x 400…1150, y 3700…4450).

					Проект: Квартира 65 м²
	Лист	№ док.	Подпись	Дата	Ваш проект на одной странице
Дизайнер	Кырлан А.С.			04.11.26	

Стадия	Лист	Листов
П	2	83

Список листов

Лист	Наименование
1	Титульный лист
2	Ваш проект на одной странице
3	Список листов
4	Как читать альбом
5	План планировки от заказчика
6	План монтажный
7	Кухня (пом. 3). Монтажная схема
8	Шкафы. Монтажная схема
9	Карта покрытий стен
10	Колерная карта
11	План размещения мебели и оборудования
12	Спецификация мебели и оборудования
13	Спецификация мебели и оборудования (продолжение)
14	Ведомости изделий, техники и фурнитуры
15	План выводов сантехники
16	Схема разводки водопровода и канализации
17	Аксонометрическая схема В1 (холодное водоснабжение)
18	Аксонометрическая схема Т3 (горячее водоснабжение)
19	Аксонометрическая схема К1 (канализация)
20	Развёртки мокрых зон: выводы ВК. Кухня-гостиная
21	Развёртки мокрых зон: выводы ВК. Санузел
22	Развёртки мокрых зон: выводы ВК. Ванная (лист 1 из 2)
23	Развёртки мокрых зон: выводы ВК. Ванная (лист 2 из 2)
24	Спецификация сантехнического оборудования
25	Раскладка плитки. Санузел. Развёртки стен
26	Раскладка плитки. Ванная. Развёртки стен
27	План размещения дверей
28	План потолков
29	Разрезы и узлы потолков
30	Разрезы и узлы потолков (продолжение)
31	Сечения потолков М 1:10
32	Однолинейная схема щита
33	План розеток и электровыводов
34	План слаботочных сетей
35	План освещения
36	Техническое задание на подбор светильников
37	Управление светильниками
38	План вентиляции
39	План отопления
40	План покрытий пола
41	Раскладка плитки. Планы полов
42	Раскладка плитки. Прихожая. Коридор
43	Развёртки стен А, Б. Гардеробная (пом. 1)
44	Развёртка стены Г. Гардеробная (пом. 1)
45	Развёртка стены А. Спальня (пом. 2)
46	Привязки электроточек, стена А. Спальня (пом. 2)
47	Развёртки стен Б, Г. Спальня (пом. 2)
48	Развёртка стены В. Спальня (пом. 2)
49	Развёртка стены В. Кухня-гостиная (пом. 3), кухонный фронт
50	Привязки электроточек и выводов ВК, стена В. Кухня-гостиная (пом. 3)
51	Развёртка стены Г. Кухня-гостиная (пом. 3), кухонный фронт
52	Привязки электроточек, стена Г. Кухня-гостиная (пом. 3)
53	Развёртки стен А1, Б1. Кухня-гостиная (пом. 3)
54	Развёртки стен А2, Б2. Кухня-гостиная (пом. 3)
55	Развёртки стен. Прихожая (пом. 4)
56	Развёртка стены А. Коридор (пом. 5)
57	Развёртки стен Б, Г. Коридор (пом. 5)
58	Развёртка стены В. Коридор (пом. 5)
59	Развёртки стен А, Б, В. Санузел (пом. 6)
60	Привязки выводов ВК, стена Б. Санузел (пом. 6)
61	Развёртка стены Г. Санузел (пом. 6)
62	Развёртки стен А, Б. Ванная (пом. 7)
63	Развёртки стен В, Г. Ванная (пом. 7)
64	Привязки электроточек и выводов ВК, стены Б, В. Ванная (пом. 7)
65	Развёртки стен. Кладовая (пом. 8)
66	Развёртка стены А. Детская (пом. 9)
67	Развёртка стены Б. Детская (пом. 9)
68	Развёртка стены В. Детская (пом. 9)
69	Привязки электроточек, стена В. Детская (пом. 9)
70	Развёртка стены Г. Детская (пом. 9)
71	Открытые вопросы, принятые допущения и конфликты. Лист 1 из 2
72	Открытые вопросы, принятые допущения и конфликты. Лист 2 из 2
Д_1	Система хранения М_01
Д_2	Шкаф-купе М_17
Д_3	Система хранения М_18
Д_4	Шкаф распашной М_19
Д_5	Кухня (пом. 3). Развёртка гарнитура
С1	Ведомость отделки помещений
С2	Спецификация отделочных материалов
С3	Спецификация отделочных материалов
С4	Список покупок
С5	Список покупок (окончание)
С6	Узлы

Общие указания

1. Размеры даны в мм от чистовых поверхностей стен: слой штукатурки 20 мм по блоку и 5 мм шпаклёвки по ГКЛ учтён. Перед заказом встроенной мебели — контрольный обмер после штукатурки.
2. Привязки мебели — от стен и углов помещения, а не от другой мебели.
3. Розетки, выводы и выключатели под мебель — см. лист 33 «План розеток и электровыводов»; сантехприборы и выводы воды — лист 15.
4. План расстановки не является документацией для изготовления мебели: изделия — по чертежам мебельщика; покупную мебель заменять только на изделия не больше габарита из спецификации (лист 12).
5. Встроенная мебель «стена в стену» — с зазором 10 мм с каждой стороны или с компенсаторами.
6. Развёртки — вид на стену изнутри помещения, по часовой стрелке; расположение стен на схеме листа развёртки; размеры — в мм по чистовым поверхностям; отметки — в м от ±0,000; высоты Н — от чистого пола помещения до оси изделия, у декора — до центра.
7. Красная цепочка — привязки электроточек и выводов по осям от угла чистовых стен; высота Н — у знака, от чистого пола до оси; высоты мебели, проёмов и границ отделки колонкой отметок слева. Стена с 5 и более точками или с мелкими звеньями привязок показана двумя видами: архитектурная развёртка (мебель, отделка, проёмы, высоты) и вид «Привязки» на отдельном листе — точки и выводы с марками, одна цепочка по осям и таблица привязок (каждая точка — строка).
8. У знака электроточки: марка (Р — розетка, S — выключатель, Св — светильник, ЭВ вывод кабеля), ×N — число постов в рамке, гр. — группа щита, Н — высота оси от чистого пола, мм; группы по клавишам выключателя — на листе выключателей.
9. Схема мебели, приборов и декора не является технической документацией для производства мебели; габариты — по паспортам изделий.
10. Марки позиций: М_NN — мебель, ОБ_NN — оборудование, С_NN — сантехника; О-N отделка (ведомость отделочных материалов, серия С).
11. Размеры мебели и изделий на заказ уточнить по месту после отделочных работ.

					Проект: Квартира 65 м²
	Лист	№ док.	Подпись	Дата	Список листов — Стадия: П; Лист: 3; Листов: 83
Дизайнер	Кырлан А.С.			04.11.26	

выпуск 04.11.2026 № 84932ed378 · стр. 3 из 83

Что в альбоме

Альбом — дизайн-проект с рабочими чертежами для ремонта. Листы идут в порядке работ: титул и вводные, реестр открытых вопросов и решений, планы (обмер, монтаж стен, мебель, двери, потолки, полы), инженерия (сантехника, электрика, вентиляция и отопление), развёртки стен с визуализациями помещений, чертежи мебели, ведомости материалов и узлы.

Вам как заказчику — титул, эта вводная, «Ваш проект на одной странице», реестр вопросов, план мебели, визуализации и развёртки, ведомости мебели и материалов. Подрядчику — всё остальное: монтажные планы, привязки выводов и розеток, узлы, ведомости объёмов.

Знаки на листах

Без знака — решение утверждено или подтверждено обмером.

Что проверить до ремонта

1. Розетки у кровати и рабочего места: хватает ли их с каждой стороны кровати и над столом (план розеток — лист 33).

2. Выводы под технику — варочная панель, духовка, посудомойка, стиральная машина, бойлер: совпадают ли с выбранными моделями (листы 12, 13, 33).

3. Высоты розеток, выключателей и выводов даны от чистого пола: если мебель или техника будут другими — скажите до штробления стен.

Номера записей

К-N — открытый вопрос: чего не хватает или что выбрать (варианты и рекомендация — в тексте). Пока ответа нет, действует строка «если решения нет».

Кф-N — конфликт между разделами (например, мебель и радиатор в одном месте); закрывается решением, которое записывается как ИЗ-N.

ИЗ-N — изменение проекта: что было, что стало и кто утвердил. Изменение без подписи предложение.

Все записи — на листе реестра сразу после вводных; на других листах на них стоят ссылки.

Почему альбом предварительный

Обмера на объекте не было: размеры взяты с плана заказчика. Технические условия (мощность, вода, вентиляция дома) не получены, часть решений ждёт вашего ответа. Пока в реестре есть открытые вопросы, альбом предварительный — пометка в штампе снимается закрытием вопросов, а не стиранием.

Правку к любому листу можно оставить по кнопке «Правка к листу» или на сайте студии: дизайн-студия-квартир.рф — укажите номер листа и что изменить.

3 круга правок входят в цену; условия — в договоре и на странице вашего заказа на сайте студии.

Шифр проекта ГД-2026-007-АИ

					Проект: Квартира 65 м²
	Лист	№ док.	Подпись	Дата	
Дизайнер	Кырлан А.С.			04.11.26	Как читать альбом

Стадия	Лист	Листов
П	4	83

выпуск 04.11.2026 № 84932ed378 · стр. 4 из 83

Отметки по высоте

±0,000	чистый пол пом. 1–5, 8, 9; отсчёт высот
−0,015	чистый пол пом. 6, 7, ниже на 15 мм
−0,064	верх плиты — расчёт, не замер (задание на обмер)
сущ. пол	снимается до плиты; не замерен (задание на обмер)

Примечания


1. Размеры — в мм по чистым поверхностям стен до отделки (по плану заказчика); площади — в м² по тем же размерам. До начала работ выполнить контрольный обмер.
2. Источник плана: растровый скан плана заказчика, размеры сняты с размерных цепочек, на объекте не замерены.
3. За отметку ±0,000 принят чистый пол, не существующий (блок отметок). «Низ перекрытия» у марки помещения — отметка низа перекрытия от ±0,000, как на развёртках и плане потолков (не высота потолка: потолок — по плану потолков).
4. Толщины стен: наружные 300 мм, перегородки 120 мм; отличающиеся толщины и уступы размерами на плане.
5. Обмер — существующее положение: новых конструкций на листе нет, они — на плане монтажа.
6. Несущие стены не определены: до технического заключения все стены считать несущими; проёмы и штробы в них не выполнять.
7. Дверные проёмы показаны без заполнения (двери — лист 27); высота дверных проёмов 2100 мм, проёмов без двери 2100 мм; низ окон (подоконник) 800 мм от чистого пола, высота окон 1600 мм.
8. Диагонали — контрольные размеры; расхождение более 5 мм подписать на плане как перекос.
9. Размеры проверить на месте до начала работ; расхождение контрольных промеров ≤ 2 %.
10. Размеры короче 1 мм на листе цепочкой не показаны (две выносные линии на таком расстоянии сливаются): пом. 5, стена В — 40 мм от угла до проёма.

Экспликация помещений


№	Наименование	Площадь, м²
1	Гардеробная	4,20
2	Спальня	8,27
3	Кухня-гостиная	18,91
4	Прихожая	4,15
5	Коридор	5,51
6	Санузел	1,83
7	Ванная	3,85
8	Кладовая	2,50
9	Детская	16,02
	Итого (общая площадь)	**65,24**

Условные обозначения

- существующие стены (сечение)
- окно (рама, остекление)
- проём существующий, без заполнения (откосы)
- стояк: К1 — канализация, В1 — ХВС, Т3 — ГВС
- диагональ помещения — контроль прямоугольности
- 1 — номер помещения, площадь м²

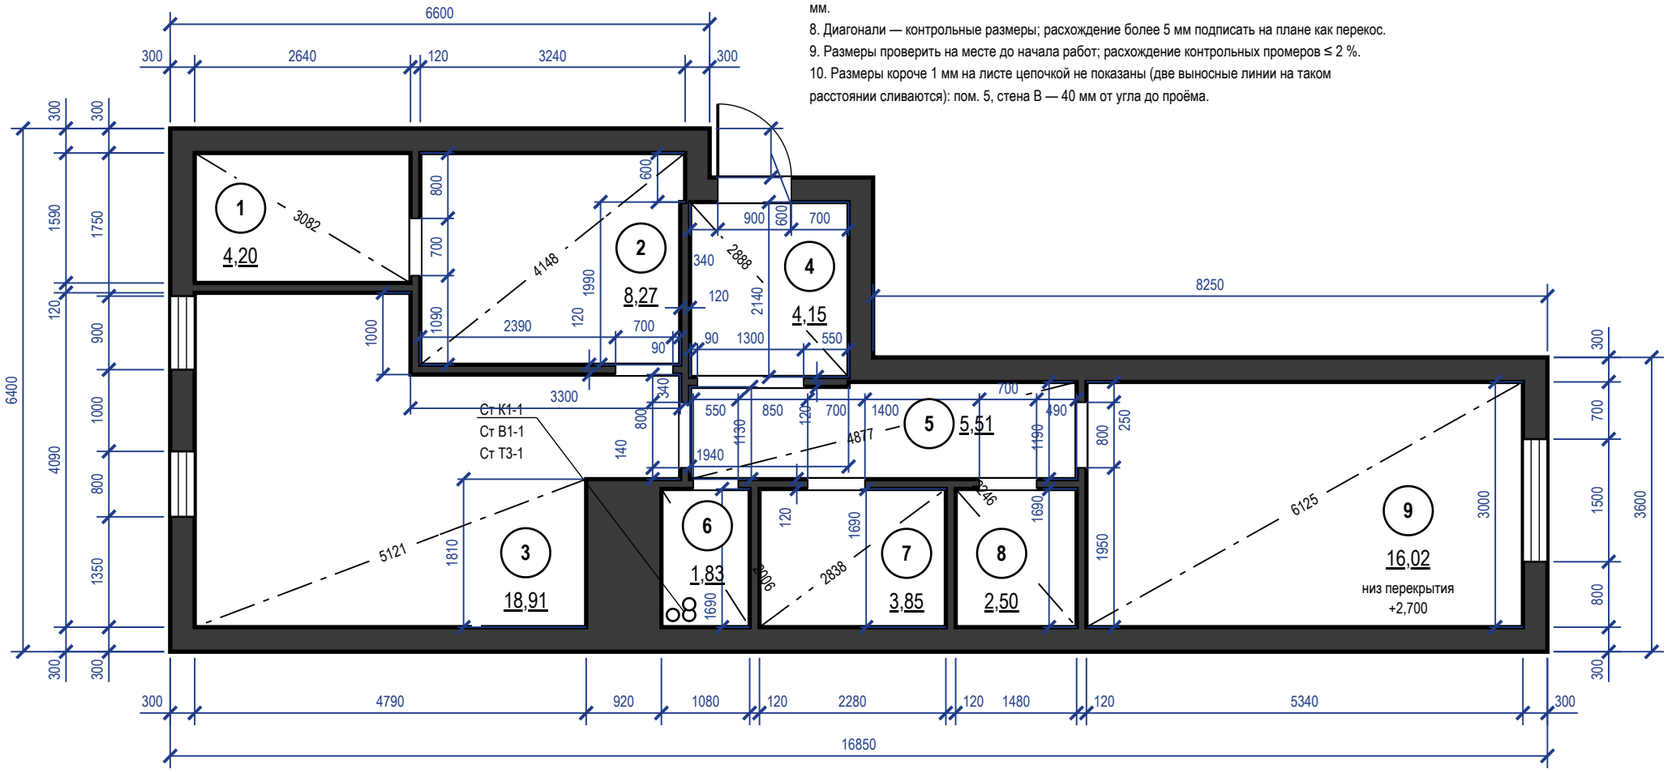

					Проект: Квартира 65 м²	**М 1:75**
	Лист	№ док.	Подпись	Дата		
Дизайнер	Кырлан А.С.			04.11.26	План планировки от заказчика	Стадия / Лист / Листов
						П / 5 / 83

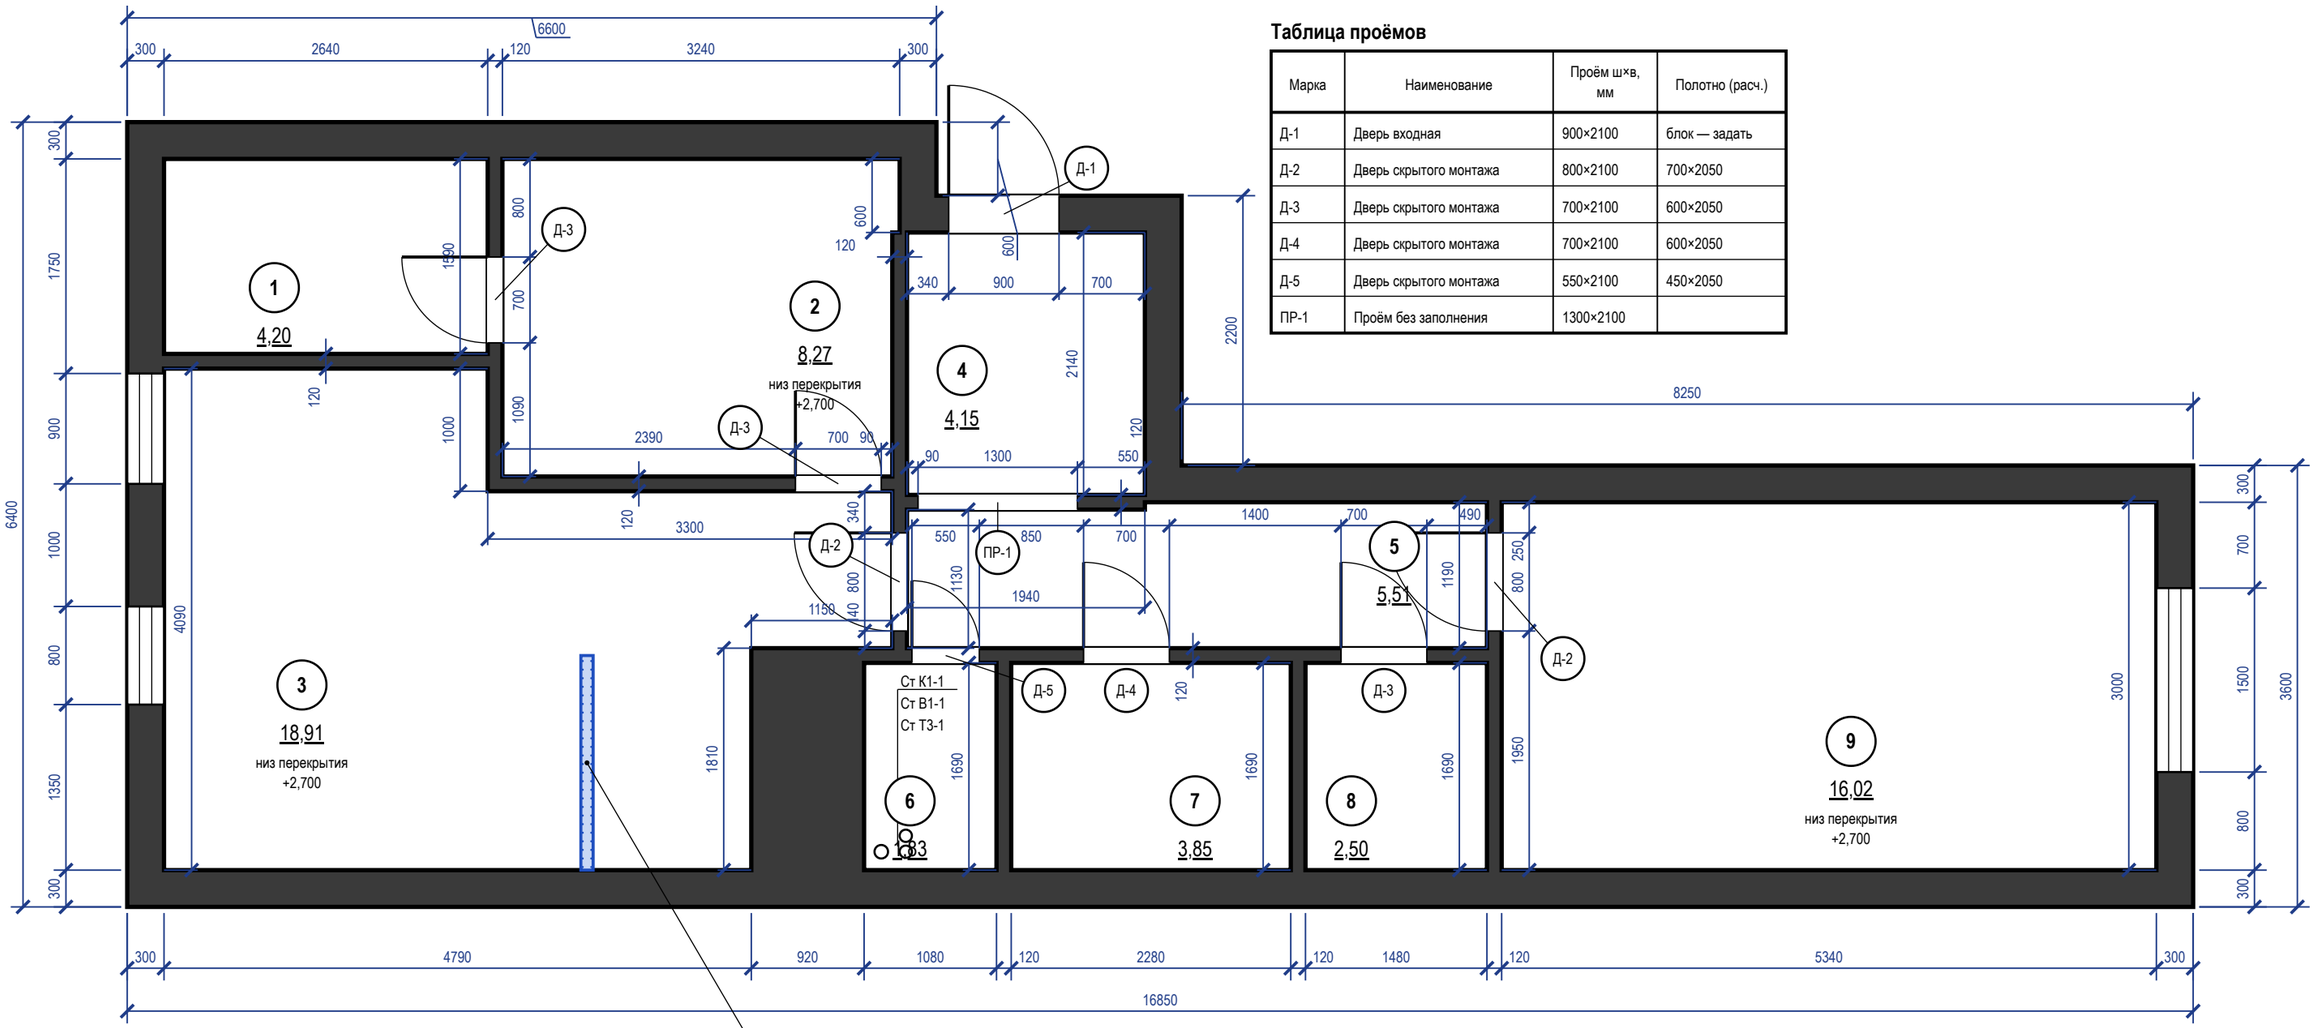

П-1 · перегородка 100 мм, до плиты

ГКЛ 2 слоя с каждой стороны по металлическому каркасу ПС 75

Таблица проёмов

Марка	Наименование	Проём ш×в, мм	Полотно (расч.)
Д-1	Дверь входная	900×2100	блок — задать
Д-2	Дверь скрытого монтажа	800×2100	700×2050
Д-3	Дверь скрытого монтажа	700×2100	600×2050
Д-4	Дверь скрытого монтажа	700×2100	600×2050
Д-5	Дверь скрытого монтажа	550×2100	450×2050
ПР-1	Проём без заполнения	1300×2100	

Экспликация помещений


№	Наименование	Площадь, м²
1	Гардеробная	4,20
2	Спальня	8,27
3	Кухня-гостиная	18,91
4	Прихожая	4,15
5	Коридор	5,51
6	Санузел	1,83
7	Ванная	3,85
8	Кладовая	2,50
9	Детская	16,02
	Итого (общая площадь)	**65,24**

Примечания


1. Размеры — в мм от чистовых поверхностей стен до отделки; размеры уточнить по месту до начала работ.
2. Новые перегородки и облицовки — синим; каркас и обшивка — по выноскам. Д-N, ПР-N в кружке — марка проёма: проём и полотно — по таблице проёмов, «расч.» — полотно по проёму, заказ по выбранной модели; ведомость, отделка и фурнитура — лист 27.
3. Несущие стены не изменять: проёмы, ниши и штробы в них — только по техническому заключению.
4. «расч.» — полотно, выведенное из проёма по запасу каталогов; заказ — по таблице проёмов выбранной модели; Д-1: входной блок по ГОСТ 31173-2016 — задать при выборе блока.
5. Размеры короче 1 мм на листе цепочкой не показаны (две выносные линии на таком расстоянии сливаются): пом. 5, стена В — 40 мм от угла до проёма.

					Проект: Квартира 65 м²	**М 1:50**
	Лист	№ док.	Подпись	Дата		
Дизайнер	Кырлан А.С.			04.11.26	План монтажный	Стадия: П; Лист: 6; Листов: 83

Привязка выводов и крепление модулей

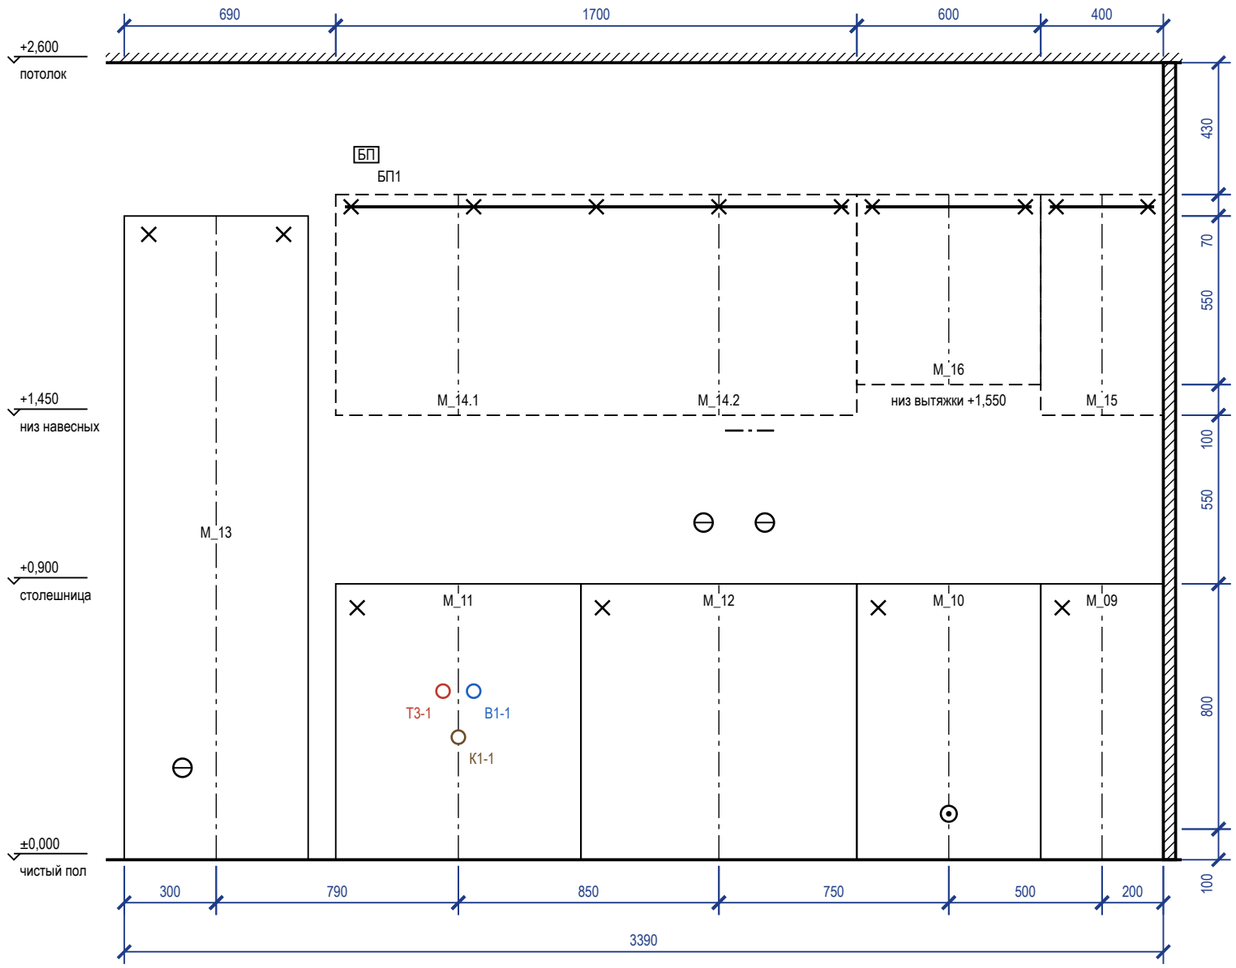

План столешницы

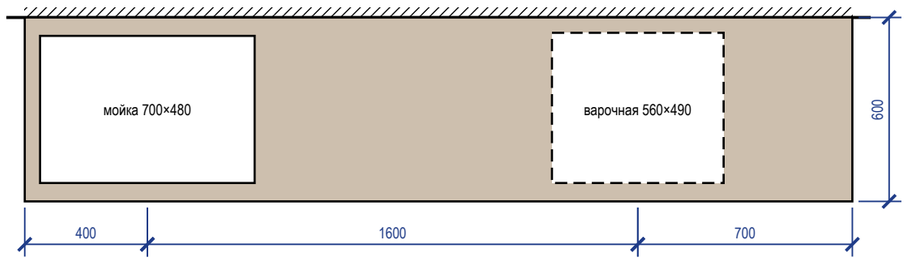

Привязка выводов к осям модулей

Код	Назначение	Модуль	От оси, мм	H, мм	Размещение
	розетка — холодильник	М_13	−110	300	за пеналом
БП1	блок питания	М_14.1	−300	2300	в навесном модуле
Т3-1	Т3 — межос. 100	М_11	−50	550	в модуле мойки
К1-1	К1 Ø50 — мойка	М_11	0	400	в модуле мойки
В1-1	В1 — межос. 100	М_11	+50	550	в модуле мойки
	розетка — рабочая зона	М_12	−50	1100	над столешницей (фартук)
	светодиодная лента — подсветка столешницы	М_12	+100	1400	в профиле по низу навесного модуля
	розетка ×2 — рабочая зона	М_12	+150	1100	над столешницей (фартук)
	вывод кабеля — варочная панель	М_10	0	150	в соседнем модуле, за ящиком

Зазоры под отделку

Поверхность	Отделка	Зазор, мм	Учесть
фартук	плитка / стеновая панель	10	от чернового основания до корпуса навесных и столешницы
стены	окраска	5	под штукатурку и шпаклёвку за пеналом
пол	инженерная доска		цоколь — после укладки пола, опоры ±20 мм

Условные обозначения


- нижний модуль, пенал (контур)
- невидимый контур: навесной модуль, корпус под столешницей
- ось модуля (от неё — привязка вывода)
- анкер / уголок крепления к стене
- розетка на стене
- вывод кабеля к технике
- B1 — вывод воды В1 / Т3, канализации К1

Примечания


1. Выводы — по проекту электрики и ВК; привязка по горизонтали — от оси модуля (плюс — вправо по виду), по высоте — от чистого пола до оси вывода.
2. Пенал — уголки к стене 2 шт. сверху; нижние модули — стяжками между собой и уголком к стене; ряд выставить по уровню опорами цоколя.
3. Розетки над столешницей — не ниже 150 мм над ней и не за корпусом техники; розетка за ПММ, духовым шкафом и холодильником — только в соседнем модуле или в зоне цоколя с доступом.
4. Столешница — вырезы по шаблонам выбранных моделей мойки и варочной панели; торцы у стены — герметик, пристеночный плинтус.

					Проект: Квартира 65 м²	М 1:20
	Лист	№ док.	Подпись	Дата		
Дизайнер	Кырлан А.С.			04.11.26	Кухня (пом. 3). Монтажная схема	Стадия: П; Лист: 7; Листов: 83


Система хранения М_01 (пом. 1)

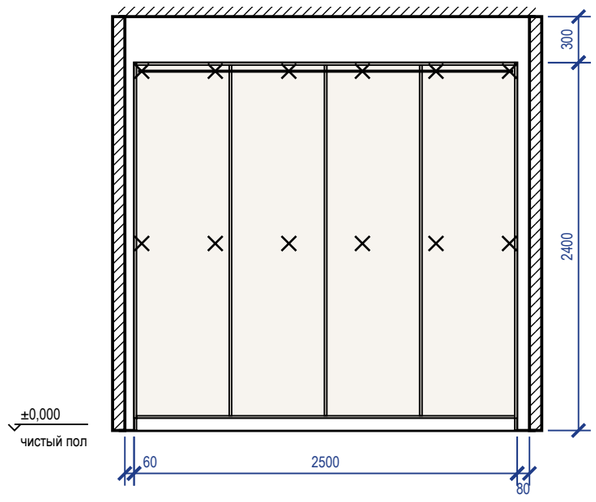


Шкаф-купе М_17 (пом. 4)

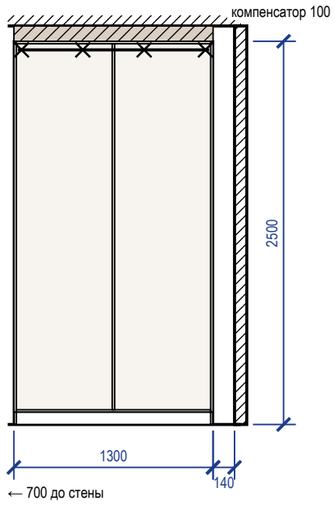

Система хранения М_18 (пом. 8)

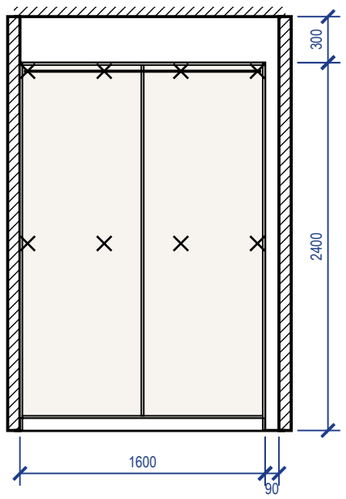

Шкаф распашной М_19 (пом. 9)

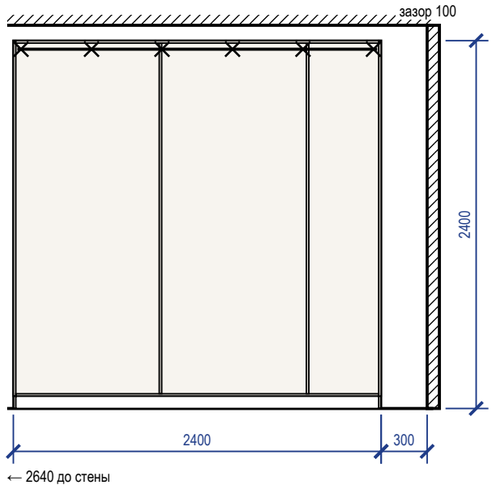

Крепление и зазоры под отделку

Марка	Помещение, стена	Основание	Отделка стены	Зазор, мм	Крепёж по планке	От опрокидывания
М_01	Гардеробная (1), стена А	по основанию — см. таблицу крепежа	окраска	5	анкер 12 шт. (2 ряда)	крепление к стене, 3 точки
М_17	Прихожая (4), стена Б	по основанию — см. таблицу крепежа	окраска	5	анкер 4 шт., шаг 400	уголки 2 шт.
М_18	Кладовая (8), стена Б	по основанию — см. таблицу крепежа	окраска	5	анкер 8 шт. (2 ряда)	уголки 2 шт.
М_19	Детская (9), стена А	по основанию — см. таблицу крепежа	окраска	5	анкер 6 шт., шаг 460	уголки 2 шт.

Крепёж по основанию стены

Основание стены	Крепёж
бетон, ж/б	анкер-шуруп 7,5×72 или дюбель 8×60 с шурупом 5×70
кирпич полнотелый	дюбель 8×80 с шурупом 5×90
газобетон, пазогребень	дюбель для газобетона 10×100 или химический анкер
гипсокартон	закладная до обшивки (брус 40×80 или фанера 18 мм), саморез в закладную

Условные обозначения

- анкер / уголок крепления к стене
- корпус и полки ЛДСП (вид на стену)
- компенсатор — короб до потолка

Примечания

1. Установочные размеры — от чистого пола и чистых стен; перед установкой контрольный замер после отделки.
2. Порядок: корпус выставить по уровню опорами цоколя → закрепить к стене по задней планке → навесить двери и фасады, отрегулировать зазоры → подогнать и закрепить компенсатор.
3. Анкеры — с шагом не более 500 мм, не ближе 50 мм от края планки; на ГКЛ только в закладную, установленную до обшивки.
4. Скрытые коммуникации под анкеры проверить детектором; трассы электрики по плану розеток.


	Лист	№ док.	Подпись	Дата
Дизайнер	Кырлан А.С.			04.11.26

Проект: Квартира 65 м² — **М 1:40**

Шкафы. Монтажная схема

Стадия	Лист	Листов
П	8	83

выпуск 04.11.2026 № 84932ed378 · стр. 8 из 83

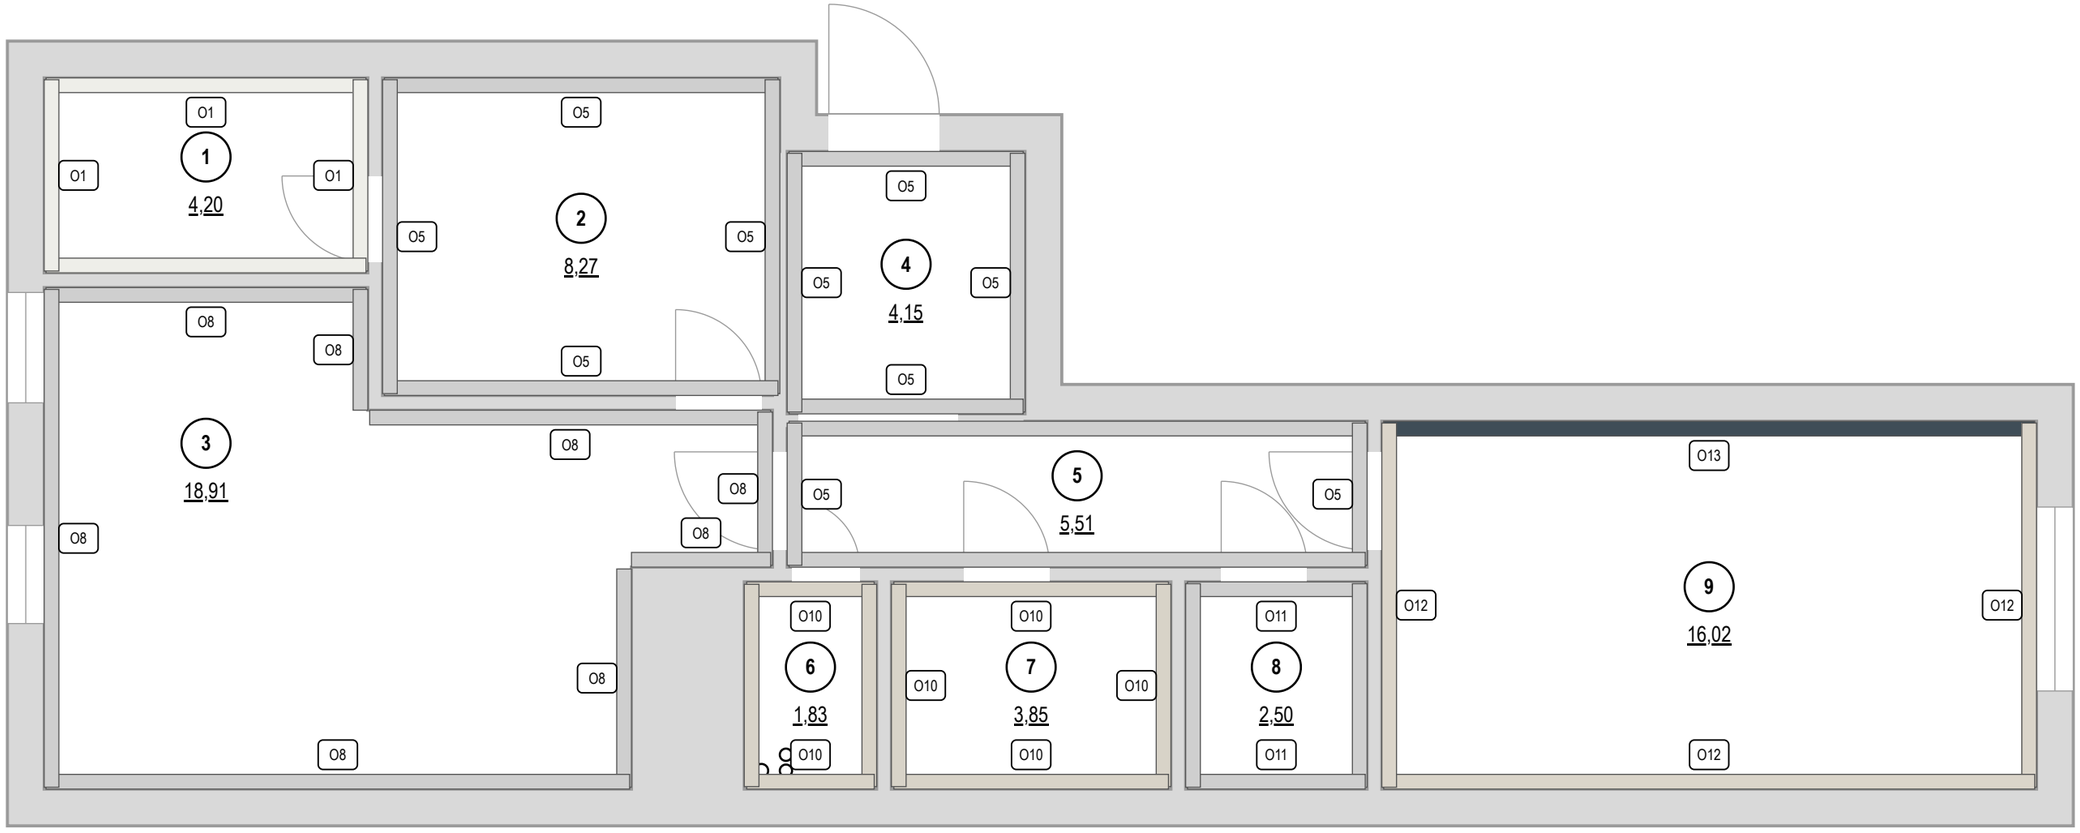

Покрытия стен

Марка	Покрытие	Помещение: S, м²	Итого, м²
O1	окраска Tikkurila · V503 «Winter»	1: 21,0	21,0
O5	окраска Tikkurila · S 1502-Y50R	2: 27,1; 4: 16,3; 5: 20,3	63,6
O8	окраска Tikkurila · S 1002-Y50R	3: 45,7	45,7
O10	облицовка плиткой Italon · 610010001195 «Charme Extra» 600×1200 мм	6: 12,9; 7: 18,9	31,8
O11	окраска Tikkurila · S 0502-Y	8: 15,3	15,3
O12	окраска Farrow & Ball · No. 241 «Skimming Stone»	9: 24,3	24,3
O13	окраска Farrow & Ball · No. 30 «Hague Blue»	9: 13,3	13,3

Площади — нетто, по развёрткам (за вычетом проёмов и фартука); высоты помещений — от чистого пола.

	Лист	№ док.	Подпись	Дата
Дизайнер	Кырлан А.С.			04.11.26

Проект: Квартира 65 м² — **М 1:50**

Карта покрытий стен

Стадия	Лист	Листов
П	9	83

Колерная карта по помещениям

Помещение	Поверхность	Образец	Поз.	Система и код цвета	Производитель, линейка / материал, артикул	Блеск	Класс истирания	LRV	Площадь
1. Гардеробная 4,2 м²	стены		**К1**	Tikkurila V503	Tikkurila · Harmony	матовая	1	86	21,4 м²
	потолок		**К2**	Tikkurila V503	Tikkurila · Anti-Reflex 2	глубокомат.	2	86	4,2 м²
	пол		**КМ1**	по образцу	Coswick · Классическая · арт. 1167-1101				4,2 м²
	плинтус		**К3**	Tikkurila V503	Orac Decor · Contour (Luxxus)			86	7,8 м
2. Спальня 8,27 м²	стены		**К4**	NCS S 1502-Y50R	Tikkurila	глубокомат.	2	72	27,4 м²
	потолок		**К5**	NCS S 0300-N	Tikkurila	глубокомат.	2	92	8,3 м²
	пол		**КМ1**	по образцу	Coswick · Классическая · арт. 1167-1101				8,3 м²
	плинтус		**К6**	NCS S 0300-N	Orac Decor · Contour (Luxxus)	полуматов.		92	10,3 м
3. Кухня-гостиная 18,91 м²	стены		**К7**	NCS S 1002-Y50R	Tikkurila	полуматов.	1	82	46,3 м²
	потолок		**К8**	NCS S 0300-N	Tikkurila	глубокомат.	1	92	18,9 м²
	пол		**КМ1**	по образцу	Coswick · Классическая · арт. 1167-1101				18,9 м²
	плинтус		**К6**	NCS S 0300-N	Orac Decor · Contour (Luxxus)	полуматов.		92	18,6 м
4. Прихожая 4,15 м²	стены		**К9**	NCS S 1502-Y50R	Tikkurila	полуматов.	1	72	16,6 м²
	потолок		**К8**	NCS S 0300-N	Tikkurila	глубокомат.	1	92	4,2 м²
	пол		**КМ2**	Королевская дорога	Kerama Marazzi · арт. SG501600R				4,2 м²
	плинтус		**К6**	NCS S 0300-N	Orac Decor · Contour (Luxxus)	полуматов.		92	6,0 м
5. Коридор 5,51 м²	стены		**К9**	NCS S 1502-Y50R	Tikkurila	полуматов.	1	72	20,6 м²
	потолок		**К8**	NCS S 0300-N	Tikkurila	глубокомат.	1	92	5,5 м²
	пол		**КМ2**	Королевская дорога	Kerama Marazzi · арт. SG501600R				5,5 м²
	плинтус		**К6**	NCS S 0300-N	Orac Decor · Contour (Luxxus)	полуматов.		92	7,0 м
6. Санузел 1,83 м²	стены		**КМ3**	Charme Extra	Italon · арт. 610010001195				13,3 м²
	потолок		**К8**	NCS S 0300-N	Tikkurila	глубокомат.	1	92	1,8 м²
	пол		**КМ2**	Королевская дорога	Kerama Marazzi · арт. SG501600R				1,8 м²
7. Ванная 3,85 м²	стены		**КМ3**	Charme Extra	Italon · арт. 610010001195				19,3 м²
	потолок		**К8**	NCS S 0300-N	Tikkurila	глубокомат.	1	92	3,9 м²
	пол		**КМ2**	Королевская дорога	Kerama Marazzi · арт. SG501600R				3,9 м²
8. Кладовая 2,5 м²	стены		**К10**	NCS S 0502-Y	Tikkurila	матовая	2	86	15,6 м²
	потолок		**К5**	NCS S 0300-N	Tikkurila	глубокомат.	2	92	2,5 м²
	пол		**КМ1**	по образцу	Coswick · Классическая · арт. 1167-1101				2,5 м²
	плинтус		**К6**	NCS S 0300-N	Orac Decor · Contour (Luxxus)	полуматов.		92	5,6 м
9. Детская 16,02 м²	стены		**К11**	Farrow & Ball No. 241	Farrow & Ball · Modern Emulsion	матовая	1	67	24,3 м²
	акцент А		**К12**	Farrow & Ball No. 30	Farrow & Ball · Modern Emulsion	матовая	1	7	13,3 м²
	потолок		**К2**	Tikkurila V503	Tikkurila · Anti-Reflex 2	глубокомат.	2	86	16,0 м²
	пол		**КМ1**	по образцу	Coswick · Классическая · арт. 1167-1101				16,0 м²
	плинтус		**К13**	Farrow & Ball No. 241	Orac Decor · Contour (Luxxus)			67	15,9 м

Схема палитры проекта

Стиль: Скандинавский · схема: нейтральная

основной	основной	основной	основной	второстепенный	второстепенный	акцентный
NCS S 1502-Y50R	**NCS S 1002-Y50R**	**NCS S 0300-N**	**Tikkurila V503**	**Farrow & Ball No. 241**	**NCS S 0502-Y**	**Farrow & Ball No. 30**
тёплый светло-серый LRV 72 стены 2,4,5	тёплый светлый грейж LRV 82 стены 3	белый LRV 92 потолок 2,3,4,5,6,7,8; плинтус 2,3,4,5,8	Winter LRV 86 стены 1; потолок 1,9; плинтус 1; текстиль/декор 9	Skimming Stone LRV 67 стены 9; плинтус 9	белый сёдзи/сиккуй — известь, васи LRV 86 стены 8	Hague Blue LRV 7 акцент 9; текстиль/декор 9

План 60/30/10

60%	30%	10%

Окраска, факт — по площади стен, акцентов, потолков

79%	16%	

окрашено всего 250,7 м²; второстепенный тон несут мебель и текстиль

Текстиль и декор в цветах вне палитры проекта

- Tikkurila H487 Pumice — пом. 9 (T7)
- Tikkurila V484 Driftwood — пом. 9 (T9)
- Farrow & Ball No. 229 Elephant's Breath — пом. 9 (T10)
- Farrow & Ball No. 47 Green Smoke — пом. 9 (T11)

Условные обозначения

- **К1** Tikkurila V503 · Winter · Harmony · матовая · кл. 1
- **К2** Tikkurila V503 · Winter · Anti-Reflex 2 · глубокомат. · кл. 2
- **К3** Tikkurila V503 · Winter · Contour (Luxxus)
- **К4** NCS S 1502-Y50R · Tikkurila · глубокомат. · кл. 2
- **К5** NCS S 0300-N · Tikkurila · глубокомат. · кл. 2
- **К6** NCS S 0300-N · Orac Decor Contour (Luxxus) · полуматов.
- **К7** NCS S 1002-Y50R · Tikkurila · полуматов. · кл. 1
- **К8** NCS S 0300-N · Tikkurila · глубокомат. · кл. 1
- **К9** NCS S 1502-Y50R · Tikkurila · полуматов. · кл. 1
- **К10** NCS S 0502-Y · Tikkurila · матовая · кл. 2
- **К11** Farrow & Ball No. 241 · Skimming Stone · Modern Emulsion · матовая · кл. 1
- **К12** Farrow & Ball No. 30 · Hague Blue · Modern Emulsion · матовая · кл. 1
- **К13** Farrow & Ball No. 241 · Skimming Stone · Contour (Luxxus)
- **КМ1** инженерная доска · 1167-1101
- **КМ2** керамогранит · SG501600R
- **КМ3** плитка · 610010001195

дерево (доска, паркет, ламинат) — рисунок досок

керамогранит, плитка, камень — сетка швов по формату

плашка не залита — цвет только по коду и вееру бренда

К — краска, КМ — отделочный материал (тон КМ — по описанию, эталон — образец материала); кл. — класс истирания (1 — самый стойкий к мытью); LRV — светлота цвета: 0 — чёрный, 100 — белый

Перечень выкрасов на согласование

№	Код	Бренд / веер	Пом. / стена	Подложка	Формат	Статус
1	V503	Tikkurila	1, 9	ГКЛ с грунтом; МДФ под эмаль	600×1000; 300×600	к выполнению
2	S 1502-Y50R	NCS Tikkurila	2, 4, 5	ГКЛ с грунтом	600×1000	к выполнению
3	S 0300-N	NCS Tikkurila	2, 3, 4, 5, 6, 7, 8	ГКЛ с грунтом; МДФ под эмаль	600×1000; 300×600	к выполнению

… ещё 4 выкрасов — в ведомости отделки

Примечания

1. Цвет на листе и на экране — ориентир. До покраски — выкрас на объекте: не меньше А3 (или лист ГКЛ), на грунте под эту краску, не на белой шпаклёвке, в 2 слоя; на обороте — код, бренд, веер, дата. Смотреть днём и вечером, рядом с образцами пола и плитки; к основному цвету стен — ещё 2 соседних оттенка. Красить только в цвет утверждённого выкраса.
2. Краску заказывать по коду из графы «Система и код цвета» у бренда этого кода, не «аналогом» другого; весь объём одного кода — одной партией, колеруемую краску — за один проход машины.
3. Площади — те же, что в ведомости отделки (лист С1); сколько краски заказать — в спецификации отделочных материалов (лист С2).

					Проект: Квартира 65 м²
	Лист	№ док.	Подпись	Дата	Колерная карта
Дизайнер	Кырлан А.С.			04.11.26	


Стадия	Лист	Листов
П	10	83

Экспликация помещений

лист 5 · на плане — номера в марках

Ведомость мебели и оборудования

25 позиц. (27 шт.) — расшифровка марок:
полностью на листе 12 «Спецификация мебели и оборудования»
марка, наименование, Ш×Г×В, материал, модель,
допуск замены. Марки на плане — по ней.

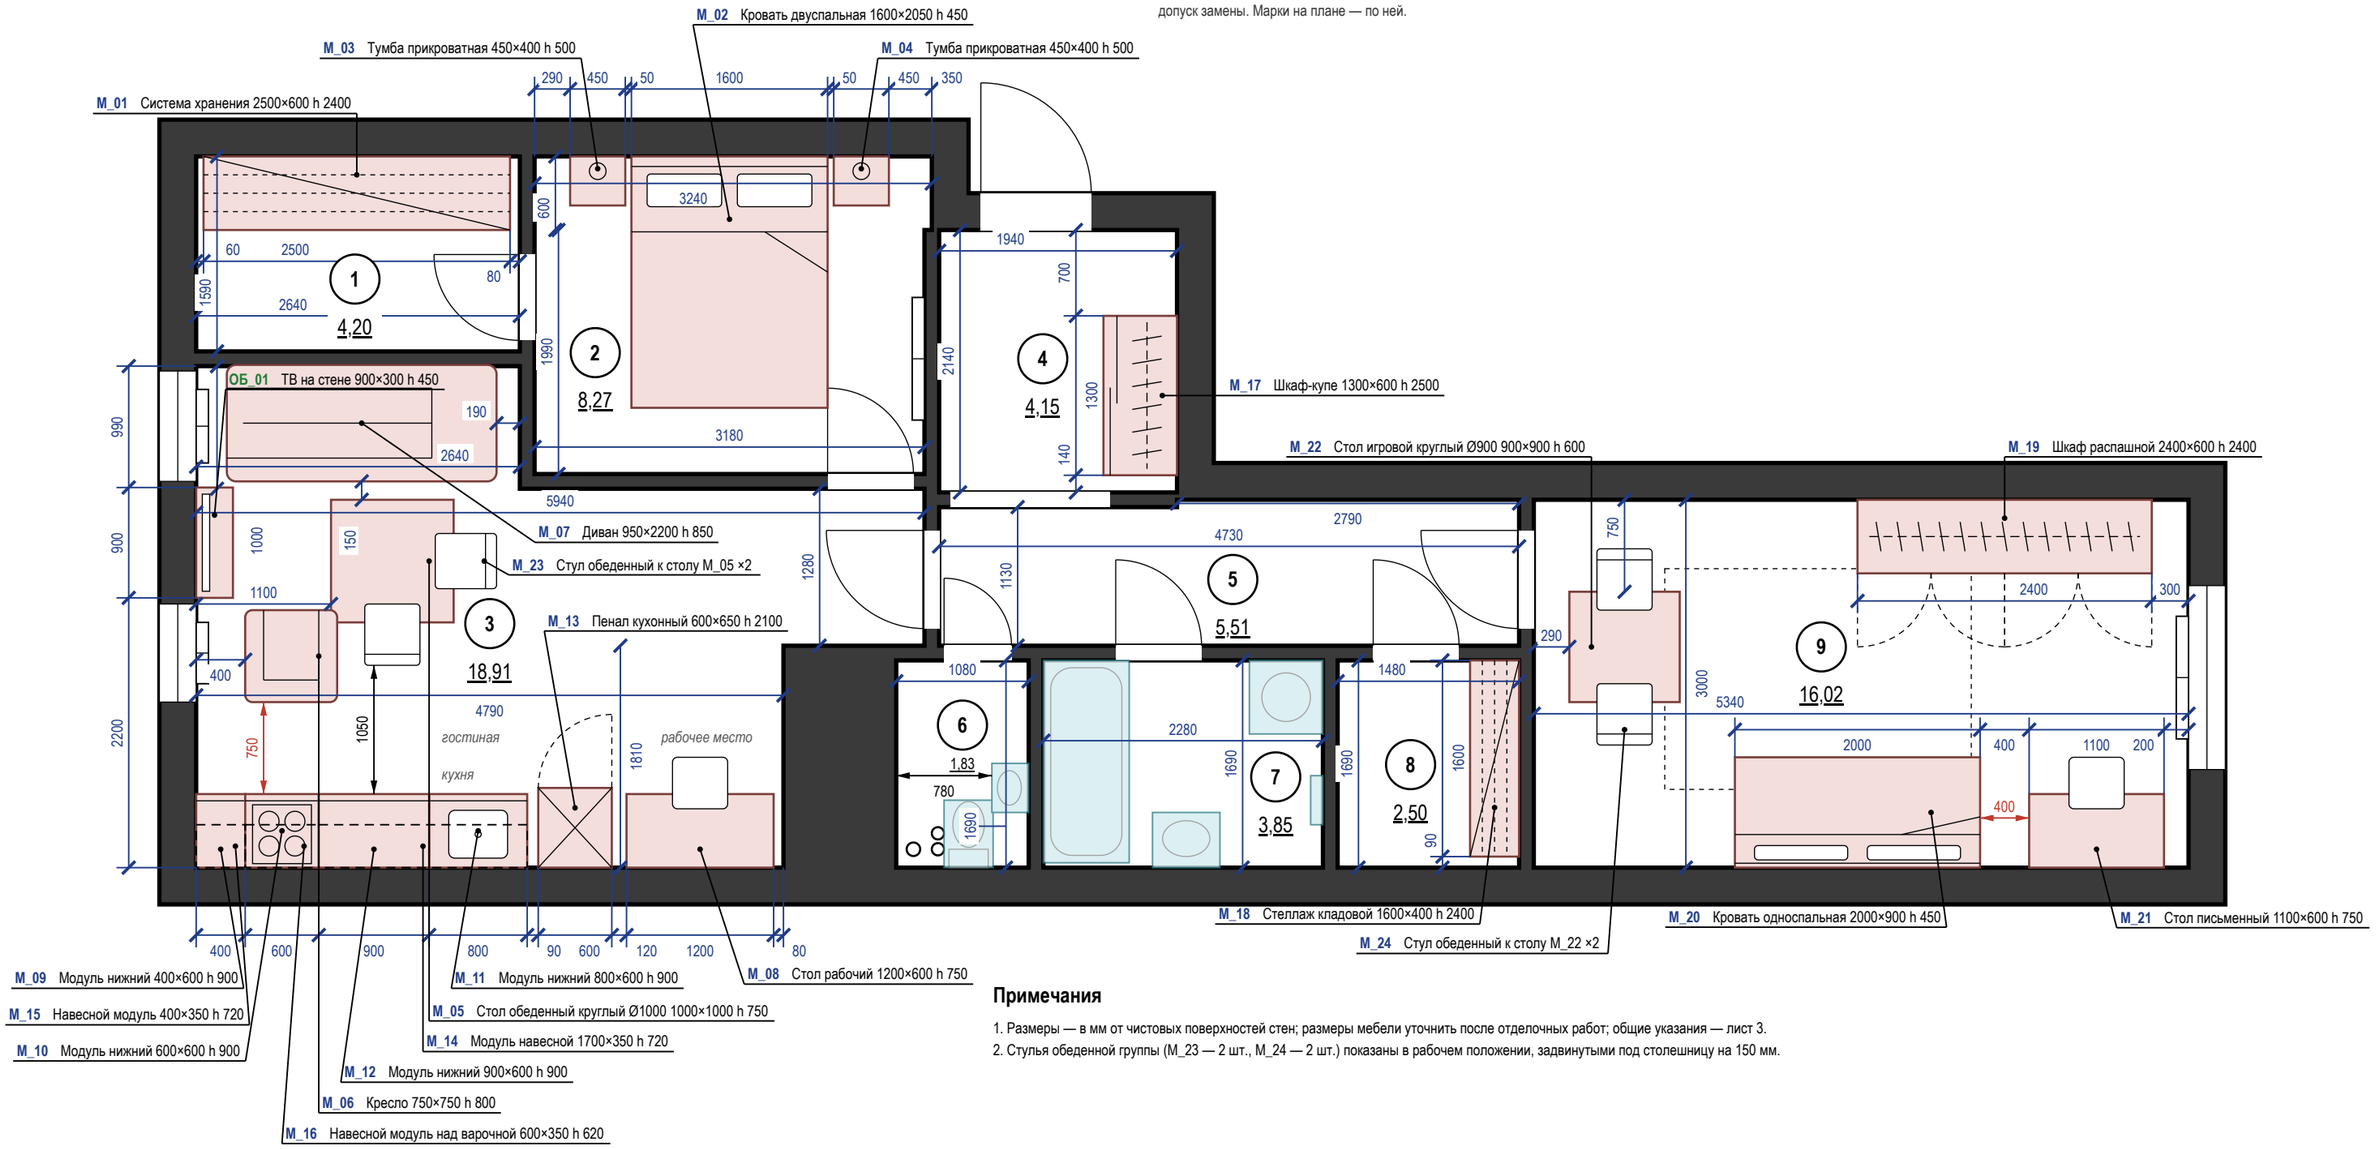

Примечания

1. Размеры — в мм от чистовых поверхностей стен; размеры мебели уточнить после отделочных работ; общие указания — лист 3.
2. Стулья обеденной группы (M_23 — 2 шт., M_24 — 2 шт.) показаны в рабочем положении, задвинутыми под столешницу на 150 мм.

					Проект: Квартира 65 м²	М 1:50
	Лист	№ док.	Подпись	Дата	План размещения мебели и оборудования	
Дизайнер	Кырлан А.С.			04.11.26	Стадия: П	Лист: 11 / Листов: 83

Поз.	Наименование и техническая характеристика	Тип, марка, обозначение документа, опросного листа	Код продукции	Поставщик	Ед. измерения	Кол.	Масса 1 ед., кг	Примечание
	Мебель встроенная и корпусная (изготовление по чертежам мебельщика)							
М_01	Система хранения: штанги, полки, ящики; каркас и полки — ЛДСП 16 мм, декор «дуб натуральный»; без фасадов; Ш×Г×В 2500×600×2400 мм			изготовление на заказ	шт.	1		пом. 1; крепление к стене
М_09	Модуль нижний; корпус ЛДСП 16 мм; фасады — МДФ эмаль 18 мм; Ш×Г×В 400×600×900 мм			изготовление на заказ	шт.	1		пом. 3
М_10	Модуль нижний, варочная; корпус ЛДСП 16 мм; фасады — МДФ эмаль 18 мм; Ш×Г×В 600×600×900 мм			изготовление на заказ	шт.	1		пом. 3
М_11	Модуль нижний, мойка; корпус ЛДСП 16 мм; фасады — МДФ эмаль 18 мм; Ш×Г×В 800×600×900 мм			изготовление на заказ	шт.	1		пом. 3
М_12	Модуль нижний; корпус ЛДСП 16 мм; фасады — МДФ эмаль 18 мм; Ш×Г×В 900×600×900 мм			изготовление на заказ	шт.	1		пом. 3
М_13	Пенал кухонный, холодильник; корпус ЛДСП 16 мм; фасады — без фасада (прибор отдельностоящий); Ш×Г×В 600×650×2100 мм			изготовление на заказ	шт.	1		пом. 3
М_14	Модуль навесной; корпус ЛДСП 16 мм; фасады — МДФ эмаль 18 мм; Ш×Г×В 1700×350×720 мм			изготовление на заказ	шт.	1		пом. 3
М_15	Навесной модуль; корпус ЛДСП 16 мм; фасады — МДФ эмаль 18 мм; Ш×Г×В 400×350×720 мм			изготовление на заказ	шт.	1		пом. 3
М_16	Навесной модуль над варочной, вытяжка встраивается в дно; корпус ЛДСП 16 мм; фасады — МДФ эмаль 18 мм; Ш×Г×В 600×350×620 мм			изготовление на заказ	шт.	1		пом. 3
М_17	Шкаф-купе; корпус ЛДСП 16 мм; фасады — ЛДСП 10 мм в алюминиевом профиле; Ш×Г×В 1300×600×2500 мм			изготовление на заказ	шт.	1		пом. 4
М_18	Стеллаж кладовой; каркас и полки — ЛДСП 16 мм, декор «дуб натуральный»; без фасадов; Ш×Г×В 1600×400×2400 мм			изготовление на заказ	шт.	1		пом. 8
М_19	Шкаф распашной; корпус ЛДСП 16 мм; фасады — МДФ 18 мм, эмаль матовая; цвет фасадов — в цвет стен (Farrow & Ball No. 241); Ш×Г×В 2400×600×2400 мм			изготовление на заказ	шт.	1		пом. 9
	Мебель покупная							
М_02	Кровать двуспальная; мягкое изголовье, обивка — ткань, цвет Farrow & Ball No. 241; Ш×Г×В 1600×2050×450 мм			аналог по характеристикам	шт.	1		пом. 2; замена ≤ габарита
М_03, М_04	Тумба прикроватная; шпон, дуб натуральный, матовое масло; Ш×Г×В 450×400×500 мм			аналог по характеристикам	шт.	2		пом. 2; замена ≤ габарита
М_05	Стол обеденный круглый Ø1000; шпон, дуб натуральный, матовое масло; Ш×Г×В 1000×1000×750 мм			аналог по характеристикам	шт.	1		пом. 3; замена ≤ габарита
М_06	Кресло; обивка — ткань, цвет Farrow & Ball No. 241; Ш×Г×В 750×750×800 мм			аналог по характеристикам	шт.	1		пом. 3; замена ≤ габарита
М_07	Диван; обивка — ткань, цвет Farrow & Ball No. 241; Ш×Г×В 950×2200×850 мм			аналог по характеристикам	шт.	1		пом. 3; замена ≤ габарита
М_08	Стол рабочий (кабинет); шпон, дуб натуральный, матовое масло; Ш×Г×В 1200×600×750 мм			аналог по характеристикам	шт.	1		пом. 3; замена ≤ габарита
М_23	Стул обеденный к столу М_05; обивка — ткань, цвет Farrow & Ball No. 241; каркас — дуб натуральный; Ш×Г×В 450×500×820 мм			аналог по характеристикам	шт.	2		пом. 3; замена ≤ габарита
ОБ_01	ТВ на стене, тумба подвесная; шпон, дуб натуральный, матовое масло; Ш×Г×В 900×300×450 мм			аналог по характеристикам	шт.	1		пом. 3; замена ≤ габарита
М_20	Кровать односпальная 900×2000; мягкое изголовье, обивка — ткань, цвет Farrow & Ball No. 241; Ш×Г×В 2000×900×450 мм			аналог по характеристикам	шт.	1		пом. 9; замена ≤ габарита
М_21	Стол письменный; шпон, дуб натуральный, матовое масло; Ш×Г×В 1100×600×750 мм			аналог по характеристикам	шт.	1		пом. 9; замена ≤ габарита
М_22	Стол игровой круглый Ø900; шпон, дуб натуральный, матовое масло; Ш×Г×В 900×900×600 мм			аналог по характеристикам	шт.	1		пом. 9; замена ≤ габарита

Примечания

1. Позиции мебели совпадают с марками на плане расстановки; размеры Ш×Г×В — Ш вдоль стены, Г от стены.
2. Размеры и привязки плана расстановки — в мм от чистовых поверхностей стен: слой штукатурки 20 мм по блоку и 5 мм шпаклёвки по ГКЛ учтён; привязки — от стен и углов помещения, а не от другой мебели.
3. План расстановки не является документацией для изготовления мебели. Встроенная и корпусная мебель изготавливается по чертежам мебельщика после контрольного обмера (после штукатурки); «стена в стену» — с зазором 10 мм с каждой стороны или с компенсаторами; графы «Тип, марка» и «Код продукции» для неё не заполняются (ГОСТ 21.110-2013).
4. Покупные изделия — аналог по характеристикам: заменять только на изделия не больше указанного габарита и того же материала и цвета.
5. Материал и цвет, не указанные в данных изделия, приняты по концепции: тон дерева — по полу, обивка — по вторичному цвету палитры; образцы согласовать до заказа.
6. Масса 1 ед. для изделий до 25 кг не указывается. Техника — по монтажным схемам изготовителя; выводы — по листам ЭОМ и ВК.

					Проект: Квартира 65 м²
	Лист	№ док.	Подпись	Дата	Спецификация мебели и оборудования
Дизайнер	Кырлан А.С.			04.11.26	

Стадия	Лист	Листов
П	12	83

Поз.	Наименование и техническая характеристика	Тип, марка, обозначение документа, опросного листа	Код продукции	Поставщик	Ед. измерения	Кол.	Масса 1 ед., кг	Примечание
M_24	Стул обеденный к столу M_22; обивка — ткань, цвет Farrow & Ball No. 241; каркас — дуб натуральный; Ш×Г×В 450×500×820 мм			аналог по характеристикам	шт.	2		пом. 9; замена ≤ габарита
	Техника встраиваемая и бытовая (покупные изделия), светильники под розетки							
	Варочная панель встраиваемая, индукционная, в модуле M_10	аналог по характеристикам: индукционная 60 см, вырез 560 × 490 мм по шаблону модели		по выбору заказчика до изготовления мебели	шт.	1		пом. 3; по схеме изготовителя
	Холодильник, в модуле M_13	аналог по характеристикам: отдельностоящий, габарит — по проёму		по выбору заказчика до изготовления мебели	шт.	1		пом. 3; по схеме изготовителя
	Вытяжка встраиваемая, в модуле M_16	аналог по характеристикам: производительность — по расчёту ОВ, шум ≤ 55 дБ(А)		по выбору заказчика до изготовления мебели	шт.	1		пом. 3; по схеме изготовителя
	Стиральная машина, место по листу ВК (ОБ_02); Ш×Г 600×600 мм	аналог по характеристикам: тип загрузки — по листу ВК, в плане 600 × 600 мм (ширина × глубина), по листу ВК		по выбору заказчика до изготовления мебели	шт.	1		пом. 7; по схеме изготовителя
	Торшер, у поз. M_06; абажур — ткань или опаловое стекло; лампа 3000 K			аналог по характеристикам	шт.	1		пом. 3; розетка — по плану розеток (ЭОМ)
	Торшер, у поз. M_20; абажур — ткань или опаловое стекло; лампа 2700 K			аналог по характеристикам	шт.	1		пом. 9; розетка Р11 (ЭОМ)
	Текстиль							
T7	Портьеры-волна; лён 100 %; цвет Tikkurila H487; карниз 1820 мм, высота 2590 мм, сборка 2			аналог по характеристикам	шт.	2		пом. 9
T8	Тюль; полиэстер 100 %; цвет Tikkurila V503; карниз 1820 мм, высота 2590 мм, сборка 2,5			аналог по характеристикам	шт.	1		пом. 9
T9	Ковёр под кроватью; шерсть 100 %; цвет Tikkurila V484; 2500×1800 мм			аналог по характеристикам	шт.	1		пом. 9; с подложкой
T10	Подушки декоративные на кровать; букле (шерсть 60 %, полиэстер 40 %); цвет Farrow & Ball No. 229			аналог по характеристикам	шт.	3		пом. 9
T11	Подушки на кровать, акцент; хлопковый бархат 100 %; цвет Farrow & Ball No. 47			аналог по характеристикам	шт.	2		пом. 9
T12	Плед на кровать; шерсть мериноса 100 %; цвет Farrow & Ball No. 30			аналог по характеристикам	шт.	1		пом. 9
	Декор							
ДК3	Картина над кроватью: графика в паспарту, рама — дуб; 1000×700 мм; низ на 1300 мм от пола			аналог по характеристикам	шт.	1	4	пом. 9; крепление к стене
ДК4	Зеркало в рост в тонкой чёрной раме; рама — чёрный матовый; 600×1600 мм; низ на 300 мм от пола			аналог по характеристикам	шт.	1	12	пом. 9; крепление: анкер для пустотелых оснований, 4 шт.

					Проект: Квартира 65 м²		
	Лист	№ док.	Подпись	Дата	Спецификация мебели и оборудования (продолжение)	Стадия	Лист	Листов
Дизайнер	Кырлан А.С.			04.11.26		П	13	83

Ведомость изделий

Марка	Наименование	Пом.	Ш×Г×В, мм	Корпус	Фасад	Кромка, мм	Кол.
M_01	Система хранения	1	2500×600×2400	ЛДСП 16	без фасадов	0,4 / 2	1
M_17	Шкаф-купе	4	1300×600×2500	ЛДСП 16	ЛДСП 10 мм в алюминиевом профиле	0,4 / 1	1
M_18	Система хранения	8	1600×400×2400	ЛДСП 16	без фасадов	0,4 / 2	1
M_19	Шкаф распашной	9	2400×600×2400	ЛДСП 16	МДФ 18 мм, эмаль матовая	0,4 / 2	1
M_13	Место под холодильник отдельностоящий: без корпуса и фасада	3	600×650×2100 (место в ряду)	без корпуса	без фасада (прибор отдельностоящий)		
M_11	Модуль нижний: мойка	3	800×600×900	ЛДСП 16	МДФ эмаль 18 мм	0,4 / 1	1
M_14	Модуль навесной: сушка, полки	3	1700×350×720	ЛДСП 16	МДФ эмаль 18 мм	0,4 / 1	1
M_12	Модуль нижний: ящики	3	900×600×900	ЛДСП 16	МДФ эмаль 18 мм	0,4 / 1	1
M_10	Модуль нижний: ящики, варочная	3	600×600×900	ЛДСП 16	МДФ эмаль 18 мм	0,4 / 1	1
M_16	Модуль навесной: полки	3	600×350×620	ЛДСП 16	МДФ эмаль 18 мм	0,4 / 1	1
M_09	Модуль нижний: ящики	3	400×600×900	ЛДСП 16	МДФ эмаль 18 мм	0,4 / 1	1
M_15	Модуль навесной: полки	3	400×350×720	ЛДСП 16	МДФ эмаль 18 мм	0,4 / 1	1

Ведомость встраиваемой техники

Поз.	Прибор	Ниша, вырез, мм	Вентиляция	Питание	Схема
M_13	Холодильник отдельностоящий	проём 600, зазор сверху ≥ 50	по паспорту модели	M_13, H=300 — за пеналом	по модели
M_11	Мойка врезная / подстольная с сифоном	вырез по шаблону, ориентир 700 × 480		смеситель — выводы ВК	по модели
M_10	Варочная панель индукционная, 60 см	вырез в столешнице 560 × 490		M_10, H=150 — в соседнем модуле, за ящиком	по модели
M_16	Вытяжка встраиваемая в навесной модуль, 60 см	низ ≥ 650 над панелью	воздуховод к вентканалу, короб до потолка	питание: точка ЭОМ не задана — вывод под прибор не делать до задания	по модели

Ведомость фурнитуры

№	Фурнитура	Тип, размер	Изделия	Кол.
1	Полкодержатель с фиксацией	ø5 мм	M_01, M_17, M_18, M_19, M_14, M_16, M_15	140
2	Штанга овальная 30×15, L = 605	+ 2 держателя	M_01	2
3	Опора регулируемая с цоколем на клипсах	ход 20 мм	M_01, M_17, M_18, M_19	30
4	Анкер по основанию стены	по таблице крепежа	M_01, M_17, M_18, M_19, M_14, M_16, M_15	39
5	Уголок крепления к стене от опрокидывания	стальной	M_01, M_17, M_18, M_19	8
6	Система дверей купе: профиль, направляющие, ролики	на 2 двери	M_17	1
7	Ручка-профиль вертикальная	в цвет профиля	M_17	2
8	Штанга овальная 30×15, L = 626	+ 2 держателя	M_17	1
9	Полка для обуви выдвижная наклонная	ширина 626	M_17	3
10	Штанга выдвижная торцевая	L по глубине	M_18	1
11	Петля накладная 110° с доводчиком	чашка 35 мм	M_19, M_11, M_14, M_16, M_15	48
12	Штанга овальная 30×15, L = 936	+ 2 держателя	M_19	2
13	Штанга овальная 30×15, L = 456	+ 2 держателя	M_19	1
14	Ручка-профиль	латунь матовая	M_11, M_14, M_12, M_10, M_16, M_09, M_15	18
15	Опора кухонная регулируемая 100–120 мм	+ клипса цоколя	M_11, M_12, M_10, M_09	20
16	Сушка для посуды в шкаф	ширина 800	M_14	1
17	Навес регулируемый для навесного шкафа	пара на секцию	M_14, M_16, M_15	4
18	Шина монтажная	L = 1640	M_14	1
19	Направляющие полного выдвижения с доводчиком NL 500	пара	M_12, M_10, M_09	9
20	Шина монтажная	L = 540	M_16	1
21	Шина монтажная	L = 340	M_15	1


Примечания

1. Модели техники выбирает заказчик до изготовления мебели; ниши, вырезы и вентиляция — по монтажной схеме выбранной модели (условие гарантии), её номер вносится в ведомость.
2. Количество фурнитуры — по чертежам изделий; запас крепежа 5 %. Аналоги — по характеристикам (доводчик, нагрузка, ход).
3. Цвет корпусов, фасадов и профилей — по колерной карте проекта. Кромка — скрытые / видимые торцы, мм.


					Проект: Квартира 65 м²
	Лист	№ док.	Подпись	Дата	Ведомости изделий, техники и фурнитуры
Дизайнер	Кырлан А.С.			04.11.26	

Стадия	Лист	Листов
П	14	83


Фрагмент 1. Кухня-гостиная (пом. 3)

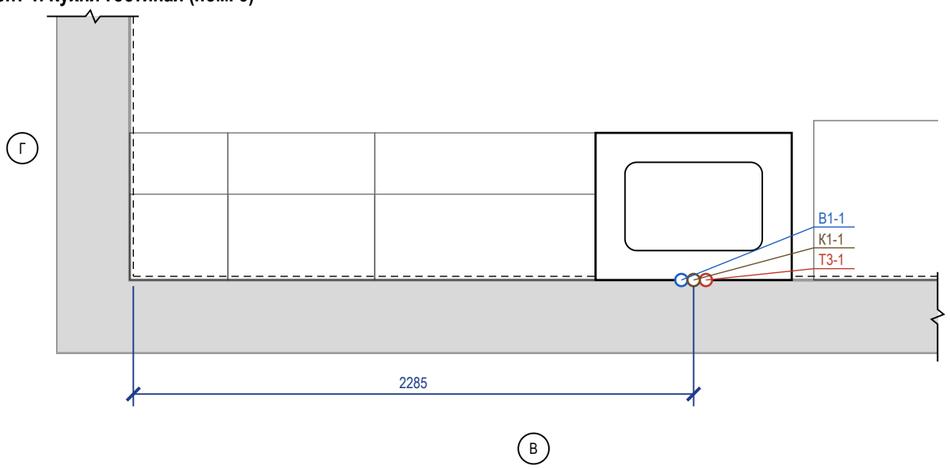

Фрагмент 2. Санузел (пом. 6)

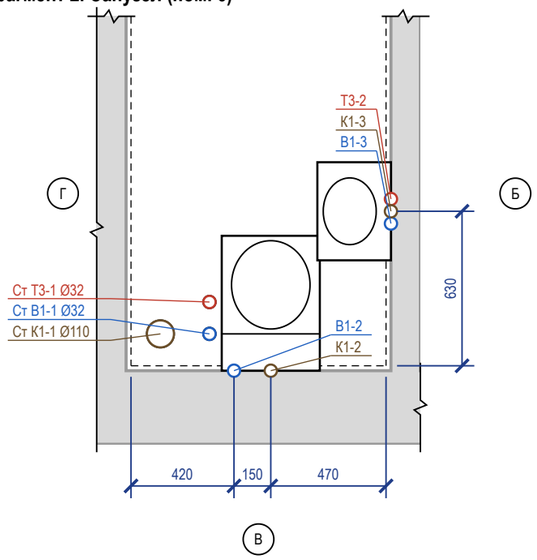

Фрагмент 3. Ванная (пом. 7)

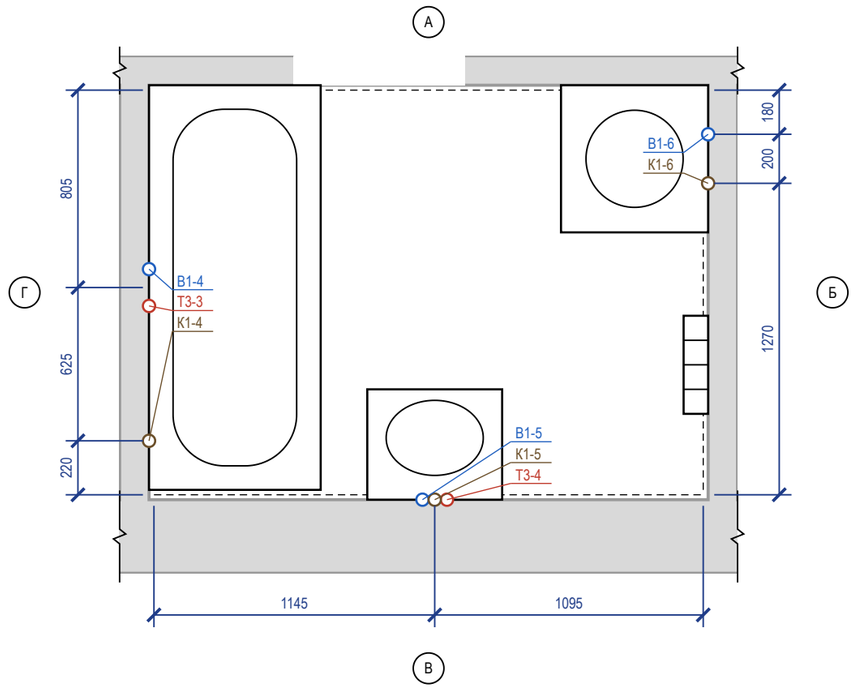

Ведомость привязок выводов

Код	Прибор	Ø	H, мм	Привязка от чист. стен, мм	Прим.
В1-1	С_01 мойка кухонная	½"	550	ст. В: 2235 от Г	межос. 100
Т3-1	С_01 мойка кухонная	½"	550	ст. В: 2335 от Г	межос. 100
К1-1	С_01 мойка кухонная	Ø50	400	ст. В: 2285 от Г	
В1-2	С_02 унитаз подвесной	½"	1000	ст. В: 420 от Г	в раме инсталляции
К1-2	С_02 унитаз подвесной	Ø110	220	ст. В: 470 от Б	
В1-3	С_03 умывальник	½"	550	ст. Б: 580 от В	межос. 100
Т3-2	С_03 умывальник	½"	550	ст. Б: 680 от В	межос. 100
К1-3	С_03 умывальник	Ø50	500	ст. Б: 630 от В	
В1-4	С_04 ванна	½"	800	ст. Г: 730 от А	межос. 150
Т3-3	С_04 ванна	½"	800	ст. Г: 770 от В	межос. 150
К1-4	С_04 ванна	Ø50	50	ст. Г: 220 от В	
В1-5	С_05 умывальник	½"	550	ст. В: 1095 от Г	межос. 100
Т3-4	С_05 умывальник	½"	550	ст. В: 1045 от Б	межос. 100
К1-5	С_05 умывальник	Ø50	500	ст. В: 1095 от Б	
В1-6	ОБ_02 стиральная машина	½"	800	ст. Б: 180 от А	кран машины
К1-6	ОБ_02 стиральная машина	Ø50	600	ст. Б: 380 от А	

Условные обозначения


- вывод В1 (код — в ведомости привязок)
- вывод Т3 (код — в ведомости привязок)
- вывод К1 (код — в ведомости привязок)
- сантехприбор по расстановке (габарит модели)
- чистовая поверхность стены (от неё привязки)
- стояк «Ст К1-N / Ст В1-N» (ГОСТ 21.601), Ø мм
- линия обрыва (граница фрагмента)
- А — обозначение стены А–Г (как на развёртках)

Примечания


1. Привязки выводов даны от чистовых поверхностей стен (облицовка на сторону: кухня-гостиная — 15 мм (по данным); санузел — 20 мм (по данным); ванная — 20 мм (по данным)); эти же грани — на развёртках и в раскладке плитки. Высоты — от чистого пола помещения.
2. До черновой разводки сверить по паспорту выбранного прибора (смеситель, инсталляция, сифон).
3. Горячая вода (Т3) — слева от холодной (В1), если смотреть на прибор. Допуск установки выводов: ±5 мм в группе, ±20 мм у отдельно стоящих.
4. Расчёт систем водоснабжения и канализации и подбор оборудования выполняет проектная организация; лист задаёт места и высоты выводов.
5. Стояки в коробах/шахтах не замоноличивать; стояк К1 в коробе — звукоизоляция стояка в коробе без жёсткого контакта с трубой; к арматуре и ревизиям — люк не меньше 300×400.

					Проект: Квартира 65 м²	М 1:25
	Лист	№ док.	Подпись	Дата		
Дизайнер	Кырлан А.С.			04.11.26	План выводов сантехники	Стадия: П; Лист: 15; Листов: 83


План квартиры (М 1:400)

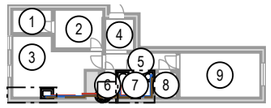


Фр. 1. Кухня-гостиная (М 1:25)

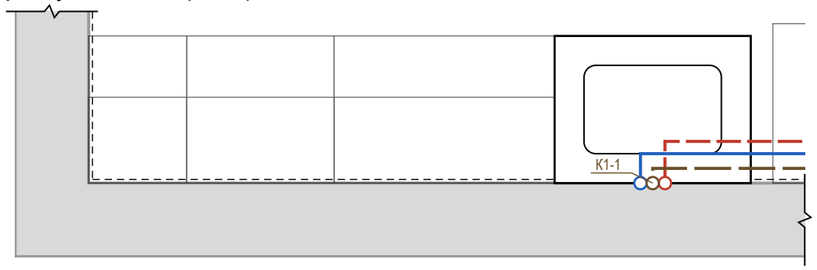

Фр. 2. Санузел (М 1:25)

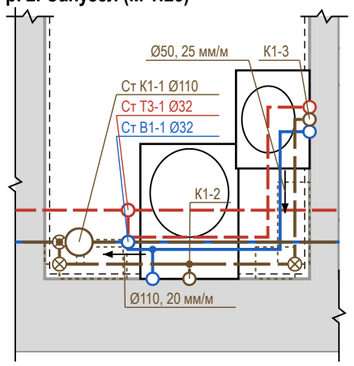

Фр. 3. Ванная (М 1:25)

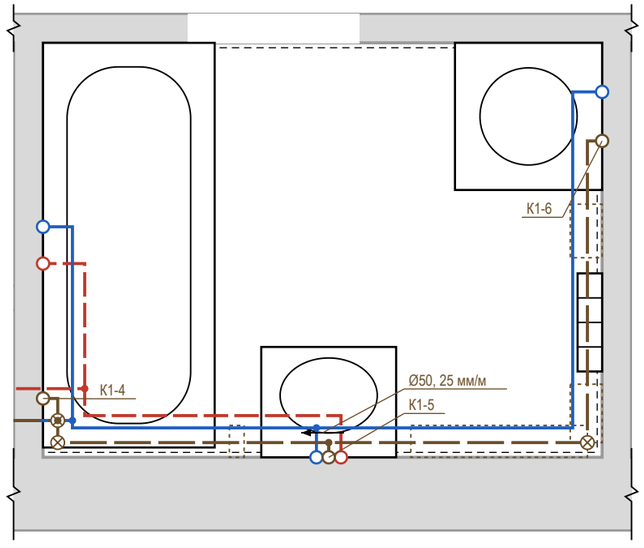

Условные обозначения


- В1 — водопровод хозяйственно-питьевой (ХВС), PP-R Ø20
- Т3 — горячее водоснабжение, подача (ГВС), PP-R Ø20
- К1 — канализация бытовая
- направление уклона К1 / пола: Ø, мм на 1 м
- ревизия (прочистка) К1 — доступ сохранить
- тройник (ответвление к прибору)
- короб К1 над чистым полом (ГКЛВ под плитку)
- вывод В1 (код — в ведомости привязок)
- вывод Т3 (код — в ведомости привязок)
- вывод К1 (код — в ведомости привязок)
- сантехприбор по расстановке (габарит модели)
- стояк «Ст К1-N / Ст В1-N» (ГОСТ 21.601), Ø мм
- линия обрыва (граница фрагмента)
- граница фрагмента на плане (Фр. N)

Профиль выпусков К1 (до врезки в стояк)

Выпуск	Прибор	Ø	L, м	i, мм/м	Δh, мм	Прокладка, мм
К1-2	С_02 унитаз подвесной	Ø110	0,76	20	15	короб 160×140
К1-6	ОБ_02 стиральная машина	Ø50	4,66	25	117	короб 200×110
К1-1	С_01 мойка кухонная	Ø50	3,70	25	93	над полом за приборами
К1-5	С_05 умывальник	Ø50	2,38	25	59	над полом за приборами
К1-3	С_03 умывальник	Ø50	1,78	25	45	короб 130×110
К1-4	С_04 ванна	Ø50	1,27	25	32	над полом за приборами

Короб h×b: h — от чистого пола, b — от чистовой стены. Стяжка 90 мм — лист полов.

Узел ввода В1, Т3 (по данным, без масштаба)

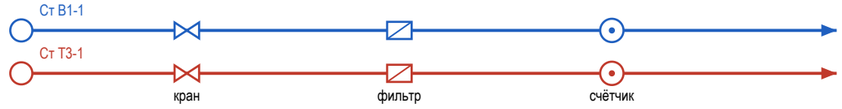

⊗ Ст К1-1: ревизия на стояке — люк в коробе


Примечания

1. Трассы принципиальные, построены от стояков вдоль стен помещений; фактическое положение фиксируется исполнительной схемой с привязками (фото с рулеткой) до закрытия.
2. Уклон К1 не менее 1/d и не более 150 мм/м (СП 30.13330.2020, п. 19.1), приняты практические уклоны; поворот — двумя отводами 45°, ревизия после поворота, доступ сохранить. Стояк К1 в коробе — звукоизоляция стояка в коробе, без жёсткого контакта короба с трубой.
3. Решение по К1: стяжка 90 мм не укрывает трубы (нужно Ø + Δh + 45 мм) — выпуски идут над чистым полом вдоль стен: К1-1, К1-5, К1-4 — за приборами и в раме инсталляции; К1-2, К1-6, К1-3 — в коробе ГКЛВ под плитку (размеры в профиле). Короба — на развёртках; отметку низа врезки в стояк замерить до черновых работ.
4. Отводы К1-6 (4,7 м) длиннее 4 м без вентиляции — у прибора воздушный клапан Ø50 в доступном месте (за люком или в тумбе) либо вентилируемый отвод (EN 12056-2, табл. 4), подбор — проектная организация.
5. Узел ввода В1, Т3 — по данным проекта: кран → фильтр → счётчик. Доступ к арматуре — через люк не меньше 300×400. Водопровод — в штробе стен или в коробах; трубы испытать давлением до закрытия (акт скрытых работ).
6. Расчёт систем, диаметры магистралей и подбор оборудования выполняет проектная организация; врезка и перенос стояков — по согласованию с управляющей организацией. Арматуру и привязки сверить по паспортам приборов.

					Проект: Квартира 65 м²
	Лист	№ док.	Подпись	Дата	Схема разводки водопровода и канализации
Дизайнер	Кырлан А.С.			04.11.26	

Стадия	Лист	Листов
П	16	83

Схема В1 (М 1:50; по вертикали и горизонтали один масштаб, глубина — ×0,5 под 45°)

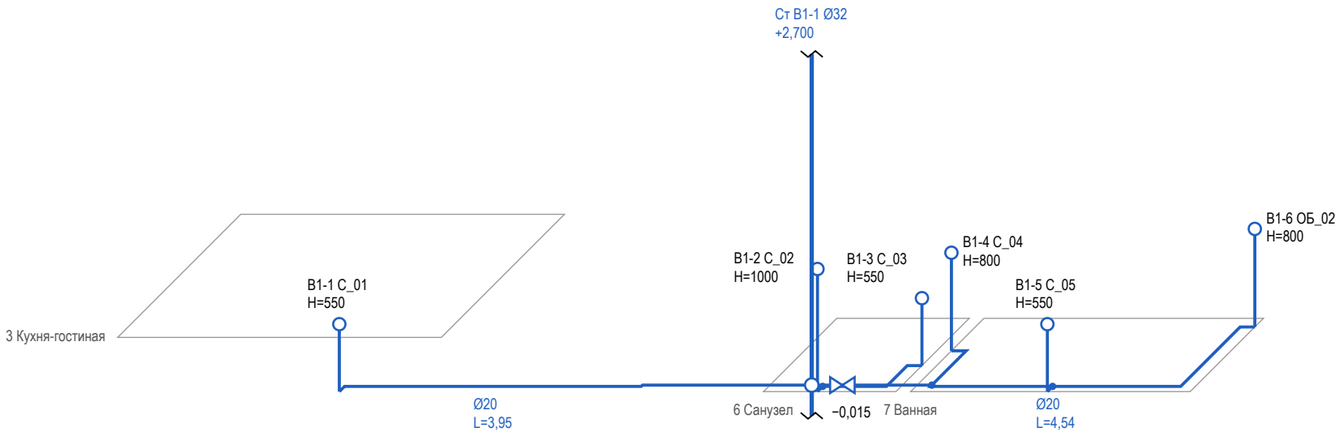

Условные обозначения


- В1 — водопровод хозяйственно-питьевой (ХВС), PP-R Ø20
- вывод В1 (код — в ведомости привязок)
- стояк «Ст К1-N / Ст В1-N» (ГОСТ 21.601), Ø мм
- стояк в плане (на отметке пола); вертикаль — стояк по высоте, разрыв — перекрытие
- тройник (ответвление к прибору)
- кран шаровой

Примечания

1. Схема В1 построена по тем же трассам, что план разводки: положение в плане сохранено, глубина — в масштабе ×0,5. Трассы принципиальные; фактическое положение фиксируется исполнительной схемой до закрытия.
2. Высоты Н — от чистого пола помещения, мм. Прокладка магистрали В1 по данным: в стяжке пола, в стяжке пола, выше плиты перекрытия; отметка трасс — по пирогу пола.
3. Узел ввода В1 (кран, фильтр, счётчик, обратный клапан, кран) — на схеме разводки; состав узла ввода — по согласованию. Кран шаровой — на первом участке от стояка.
4. Трубы испытать давлением до закрытия (акт скрытых работ, опрессовка по СП 73.13330.2016).
5. Диаметры, высоты выводов и места кранов — по паспортам выбранных приборов и расчёту проектной организации.
6. Расчёт систем, диаметры магистралей и подбор оборудования выполняет проектная организация.

					Проект: Квартира 65 м²	М 1:50
	Лист	№ док.	Подпись	Дата		
Дизайнер	Кырлан А.С.			04.11.26	Аксонометрическая схема В1 (холодное водоснабжение)	Стадия: П; Лист: 17; Листов: 83

Схема Т3 (М 1:50; по вертикали и горизонтали один масштаб, глубина — ×0,5 под 45°)

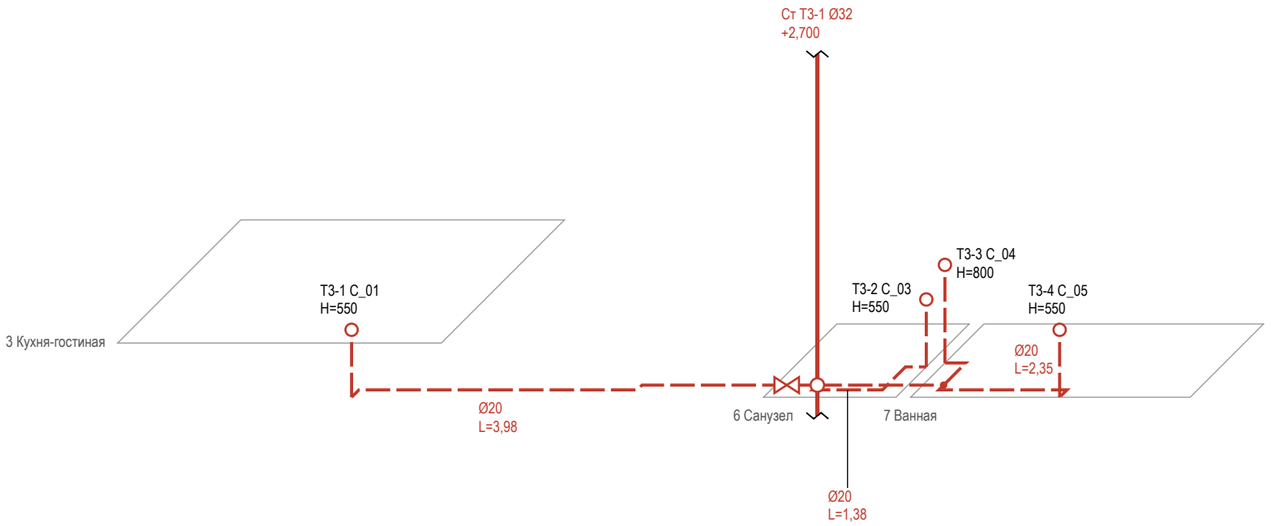

Условные обозначения


- Т3 — горячее водоснабжение, подача (ГВС), PP-R Ø20
- вывод Т3 (код — в ведомости привязок)
- стояк «Ст К1-N / Ст В1-N» (ГОСТ 21.601), Ø мм
- стояк в плане (на отметке пола); вертикаль — стояк по высоте, разрыв — перекрытие
- тройник (ответвление к прибору)
- кран шаровой

Примечания

1. Схема Т3 построена по тем же трассам, что план разводки: положение в плане сохранено, глубина — в масштабе ×0,5. Трассы принципиальные; фактическое положение фиксируется исполнительной схемой до закрытия.
2. Высоты Н — от чистого пола помещения, мм. Прокладка магистрали Т3 по данным: в стяжке пола, в стяжке пола, выше плиты перекрытия; отметка трасс — по пирогу пола.
3. Узел ввода Т3 (кран, фильтр, счётчик, обратный клапан, кран) — на схеме разводки; состав узла ввода — по согласованию. Кран шаровой — на первом участке от стояка.
4. Циркуляция ГВС в данных не задана — циркуляционного трубопровода на схеме нет.
5. Трубы испытать давлением до закрытия (акт скрытых работ, опрессовка по СП 73.13330.2016).
6. Диаметры, высоты выводов и места кранов — по паспортам выбранных приборов и расчёту проектной организации.
7. Расчёт систем, диаметры магистралей и подбор оборудования выполняет проектная организация.

					Проект: Квартира 65 м²	М 1:50
	Лист	№ док.	Подпись	Дата	Аксонометрическая схема Т3 (горячее водоснабжение)	Стадия / Лист / Листов
Дизайнер	Кырлан А.С.			04.11.26		П / 18 / 83

Схема К1 (М 1:50; по вертикали и горизонтали один масштаб, глубина — ×0,5 под 45°)

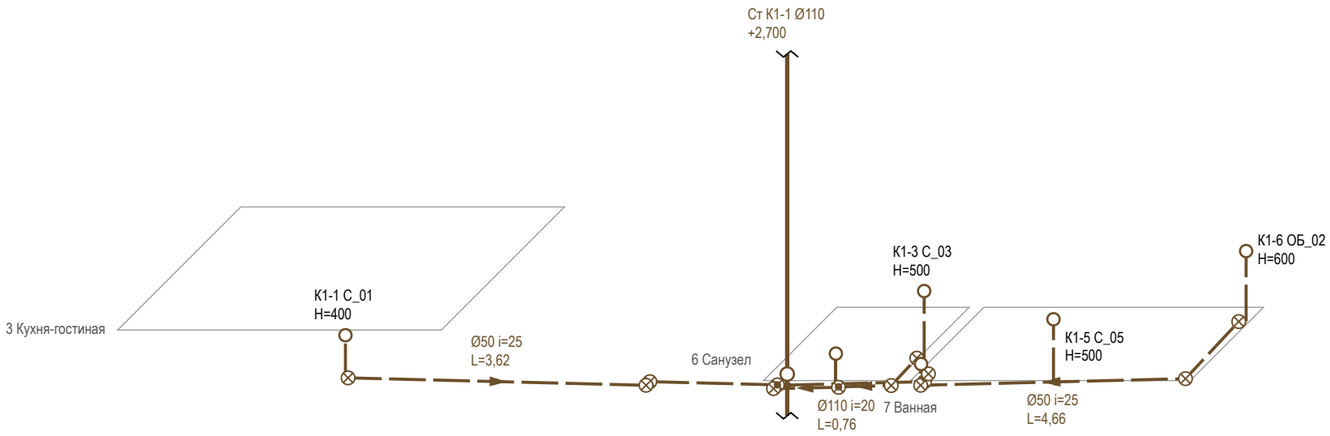

Условные обозначения

- К1 — канализация бытовая
- вывод К1 (код — в ведомости привязок)
- стояк «Ст К1-N / Ст В1-N» (ГОСТ 21.601), Ø мм
- стояк в плане (на отметке пола); вертикаль — стояк по высоте, разрыв — перекрытие
- направление уклона К1 / пола: Ø, мм на 1 м
- ревизия (прочистка) К1 — доступ сохранить
- тройник (ответвление к прибору)


Примечания

1. Схема К1 построена по тем же трассам, что план разводки: положение в плане сохранено, глубина — в масштабе ×0,5. Трассы принципиальные; фактическое положение фиксируется исполнительной схемой до закрытия.
2. Отметки — от плиты перекрытия: низ трубы у врезки в стояк — отметка из данных выпуска, к прибору труба поднимается на уклон i, мм/м (уклон не менее 1/d и не более 150 мм/м, СП 30.13330.2020, п. 19.1); чистый пол — выше плиты на стяжку (высота пирога пола). Высота выпуска прибора H — от чистого пола.
3. Ревизия — на повороте и в начале участка; стояк К1 в коробе с люком — звукоизоляция стояка в коробе; поворот — двумя отводами 45°.
4. Трубы испытать давлением до закрытия (акт скрытых работ, опрессовка по СП 73.13330.2016).
5. Диаметры, высоты выводов и места кранов — по паспортам выбранных приборов и расчёту проектной организации.
6. Расчёт систем, диаметры магистралей и подбор оборудования выполняет проектная организация.

					Проект: Квартира 65 м²	М 1:50
	Лист	№ док.	Подпись	Дата	Аксонометрическая схема К1 (канализация)	
Дизайнер	Кырлан А.С.			04.11.26		

Стадия	Лист	Листов
П	19	83

Стена В (М 1:20)

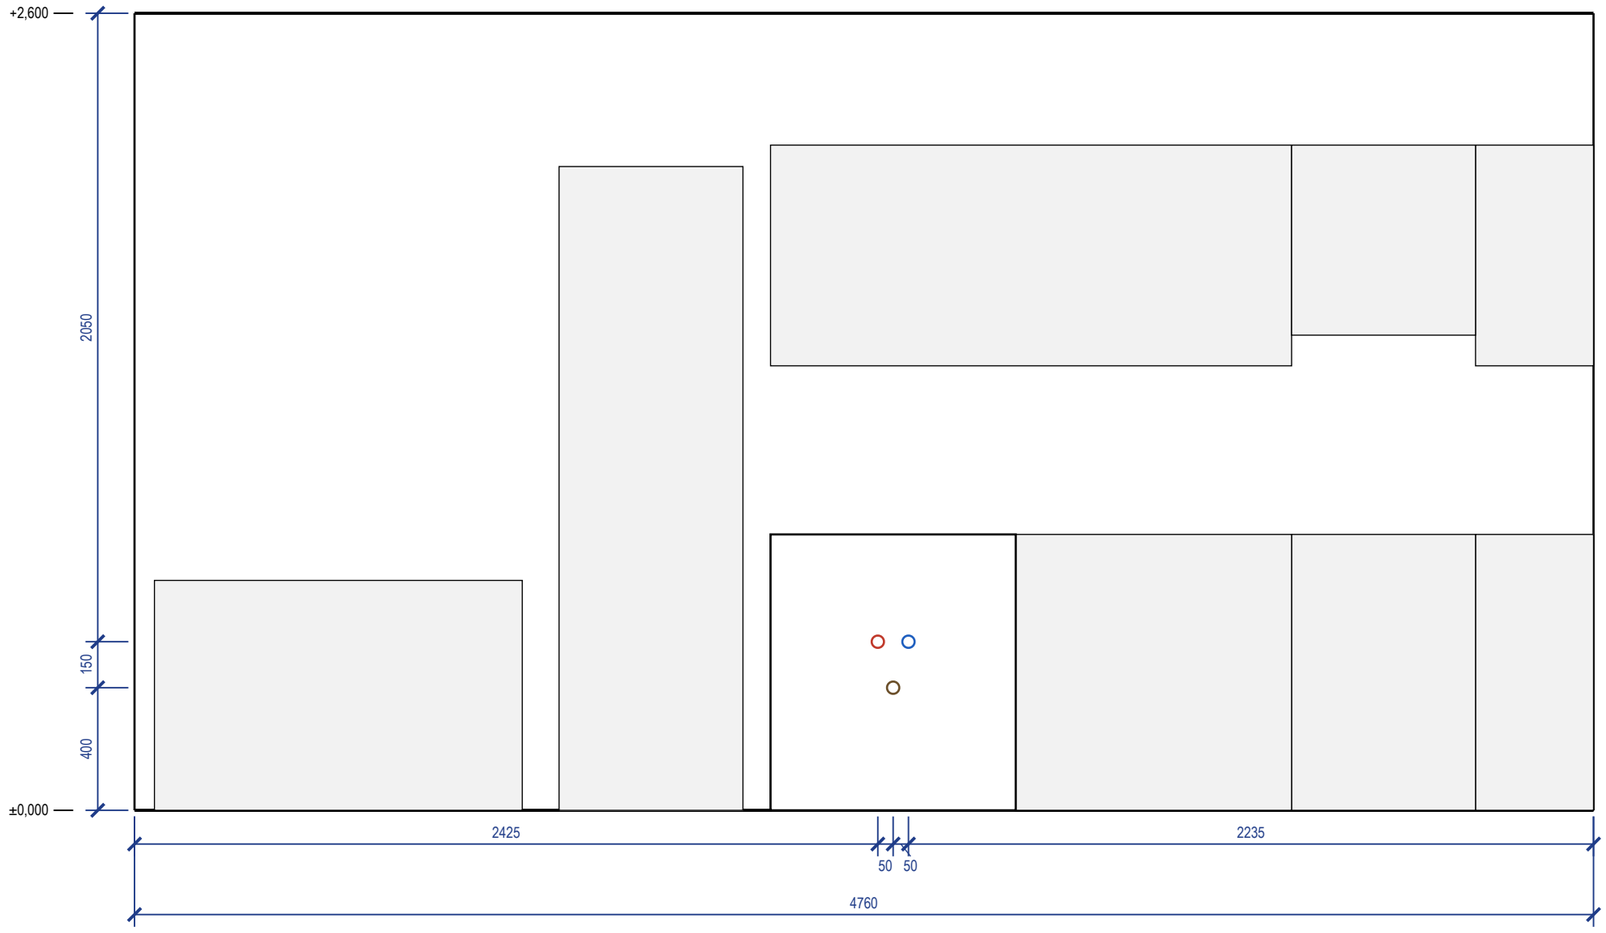

Ведомость привязок выводов (от чистого пола и угла)

Код	Прибор	Ø	H, мм	Привязка, мм
В1-1	С_01 мойка кухонная	½"	550	ст. В: 2525 от лев. угла
Т3-1	С_01 мойка кухонная	½"	550	ст. В: 2425 от лев. угла
К1-1	С_01 мойка кухонная	Ø50	400	ст. В: 2475 от лев. угла

Условные обозначения


- вывод В1 (код — в ведомости привязок)
- вывод Т3 (код — в ведомости привязок)
- вывод К1 (код — в ведомости привязок)
- сантехприбор по расстановке (габарит модели)
- дверной проём; окно — сплошной контур

Примечания


1. Габариты и высоты приборов, межосевые смесителей и места кранов — по паспортам выбранных приборов, сверяются до разметки стен.
2. Высоты H — от чистого пола помещения, мм; отметка чистого пола и потолка — у левого края вида (от ±0,000 объекта). Привязки — от левого чистового угла вида (облицовка стен вычтена), как на развёртках стен.
3. Ревизионные люки (арматура и ревизии у С_01 300×400, стена В у С_01, предложение): привязка к углу — по раскладке плитки, подтверждается обмером.
4. Ревизионные люки к арматуре и ревизиям в данных не заданы: место и размер не определены (записи реестра нет).
5. Мойка, ПММ и фильтр — выводы в шкафу мойки; диаметры и положение сифона и кранов сверить по паспортам приборов и чертежам модуля.
6. Часть подписей выводов не уместилась у знака: коды и высоты — в ведомости привязок.
7. Расчёт систем водоснабжения и канализации и подбор оборудования выполняет проектная организация; лист задаёт места и высоты выводов.

					Проект: Квартира 65 м²	М 1:20
	Лист	№ док.	Подпись	Дата		
Дизайнер	Кырлан А.С.			04.11.26	Развёртки мокрых зон: выводы ВК. Кухня-гостиная	Стадия: П; Лист: 20; Листов: 83

Стена Б (М 1:20)

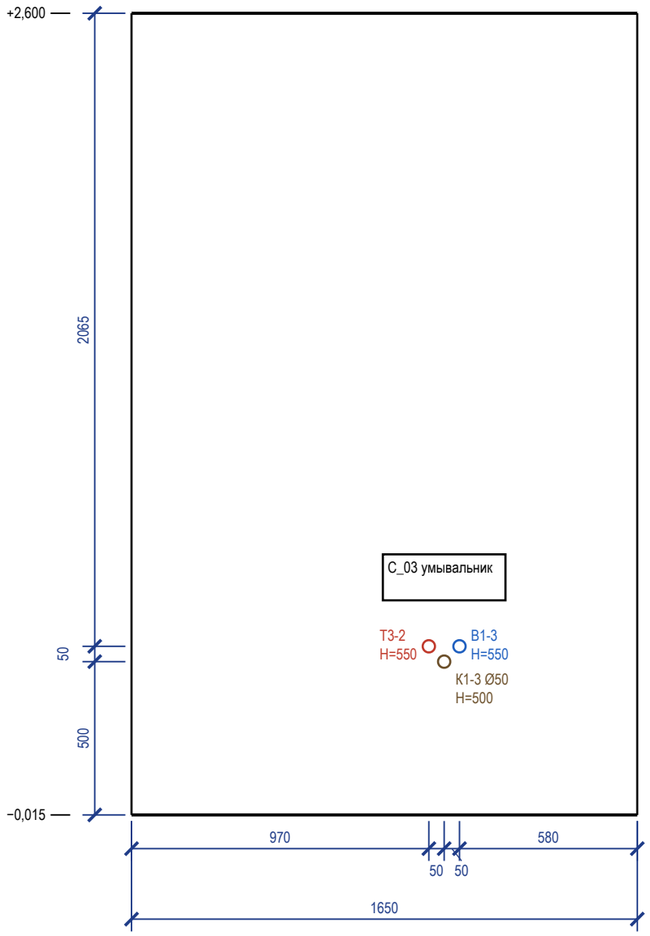

Стена В (М 1:20)

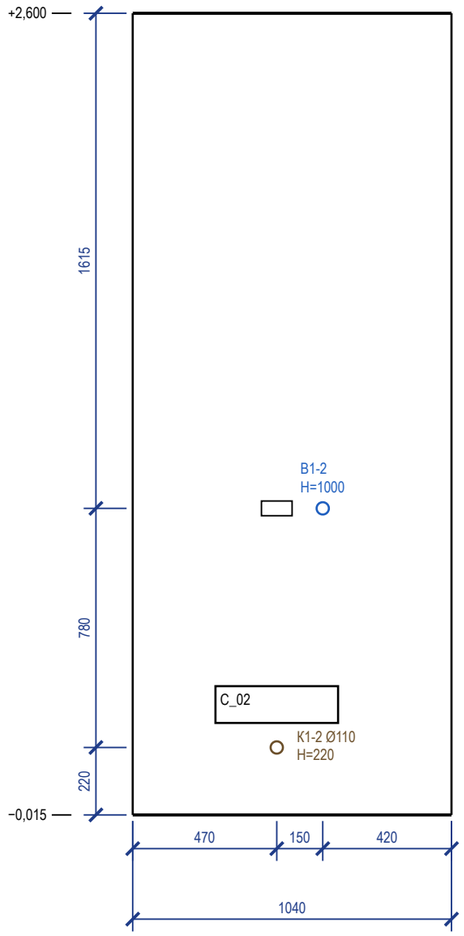

Ведомость привязок выводов (от чистого пола и угла)

Код	Прибор	Ø	H, мм	Привязка, мм
B1-3	C_03 умывальник	½"	550	ст. Б: 1070 от лев. угла
T3-2	C_03 умывальник	½"	550	ст. Б: 970 от лев. угла
K1-3	C_03 умывальник	Ø50	500	ст. Б: 1020 от лев. угла
B1-2	C_02 унитаз подвесной	½"	1000	ст. В: 620 от лев. угла
K1-2	C_02 унитаз подвесной	Ø110	220	ст. В: 470 от лев. угла

Условные обозначения


- вывод B1 (код — в ведомости привязок)
- вывод T3 (код — в ведомости привязок)
- вывод K1 (код — в ведомости привязок)
- сантехприбор по расстановке (габарит модели)
- дверной проём; окно — сплошной контур
- кнопка смыва инсталляции (H — по данным прибора)

Примечания


1. Габариты и высоты приборов, межосевые смесителей и места кранов — по паспортам выбранных приборов, сверяются до разметки стен.
2. Высоты H — от чистого пола помещения, мм; отметка чистого пола и потолка — у левого края вида (от ±0,000 объекта). Привязки — от левого чистового угла вида (облицовка стен вычтена), как на развёртках стен.
3. Кнопка смыва C_02 — H=1000 (по данным прибора).
4. Стояки в помещении: Ст К1-1 Ø110, Ст В1-1 Ø32, Ст Т3-1 Ø32 — положение на плане выводов; выводы подключаются к ним по схеме разводки.
5. Ревизионные люки (арматура и ревизии у C_02 300×400, стена В у C_02, предложение): привязка к углу — по раскладке плитки, подтверждается обмером.
6. Ревизионные люки к арматуре и ревизиям в данных не заданы: место и размер не определены (записи реестра нет).
7. Расчёт систем водоснабжения и канализации и подбор оборудования выполняет проектная организация; лист задаёт места и высоты выводов.

					Проект: Квартира 65 м²	М 1:20
	Лист	№ док.	Подпись	Дата		
Дизайнер	Кырлан А.С.			04.11.26	Развёртки мокрых зон: выводы ВК. Санузел	Стадия: П; Лист: 21; Листов: 83

Стена А (М 1:20)

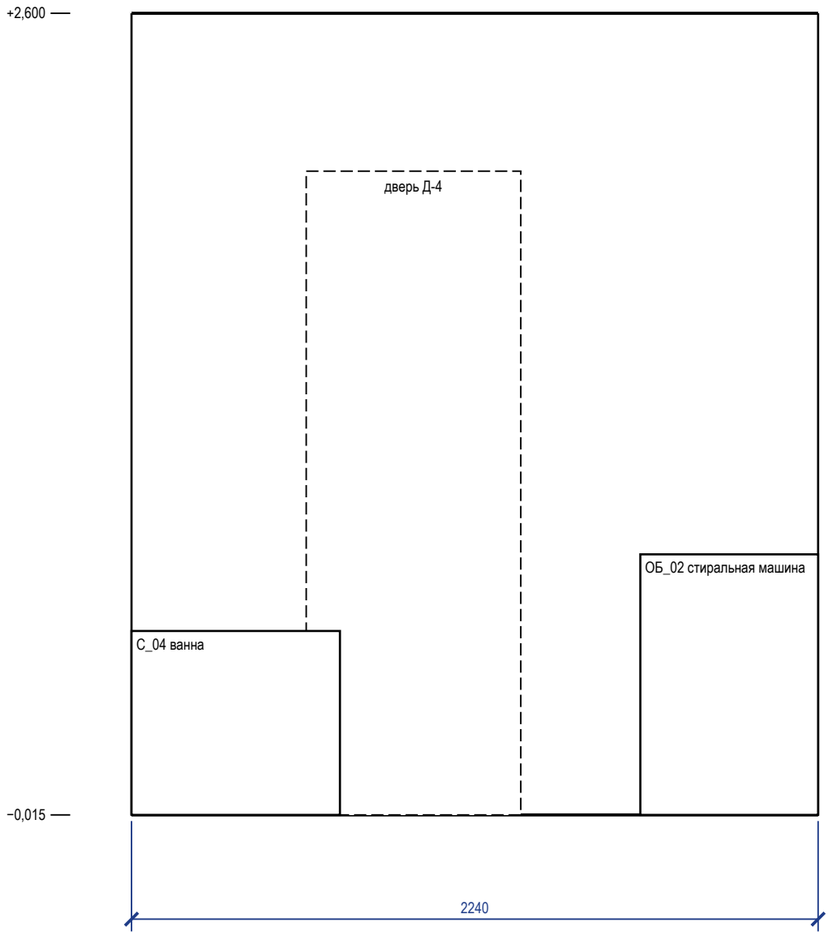

Стена Б (М 1:20)

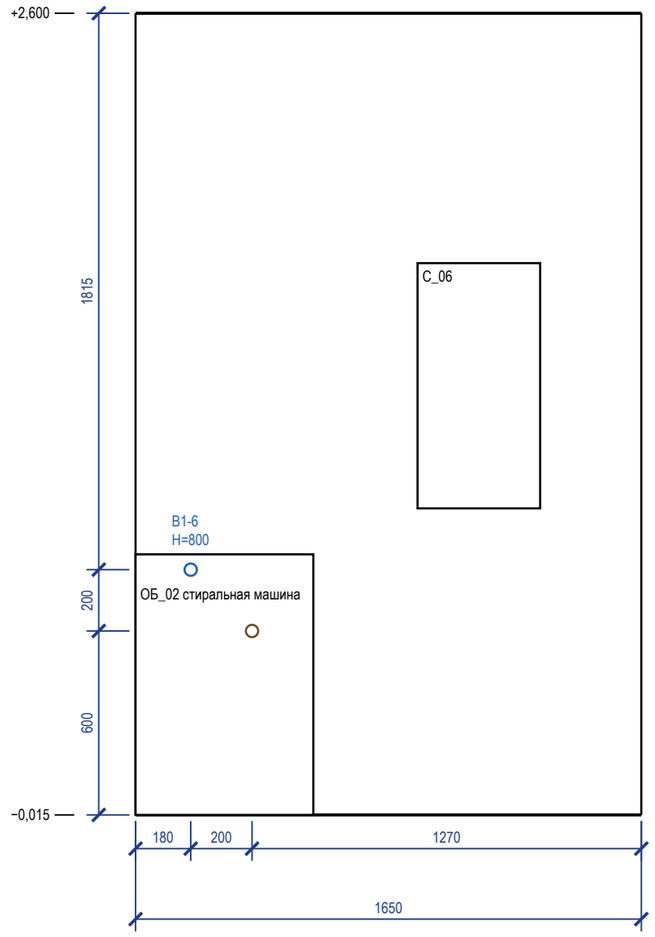

Ведомость привязок выводов (от чистого пола и угла)

Код	Прибор	Ø	H, мм	Привязка, мм
В1-6	ОБ_02 стиральная машина	½"	800	ст. Б: 180 от лев. угла
К1-6	ОБ_02 стиральная машина	Ø50	600	ст. Б: 380 от лев. угла

Условные обозначения

- вывод В1 (код — в ведомости привязок)
- вывод Т3 (код — в ведомости привязок)
- вывод К1 (код — в ведомости привязок)
- сантехприбор по расстановке (габарит модели)
- дверной проём; окно — сплошной контур


Примечания

1. Габариты и высоты приборов, межосевые смесителей и места кранов — по паспортам выбранных приборов, сверяются до разметки стен.
2. Высоты H — от чистого пола помещения, мм; отметка чистого пола и потолка — у левого края вида (от ±0,000 объекта). Привязки — от левого чистового угла вида (облицовка стен вычтена), как на развёртках стен.
3. Ревизионные люки (арматура и ревизии у С_04 300×400, стена Г у С_04, предложение): привязка к углу — по раскладке плитки, подтверждается обмером.
4. Ревизионные люки к арматуре и ревизиям в данных не заданы: место и размер не определены (записи реестра нет).
5. Часть подписей выводов не уместилась у знака: коды и высоты — в ведомости привязок.
6. Помещение «Ванная» — 2 листа: стены 1) А, Б; 2) В, Г.
7. Расчёт систем водоснабжения и канализации и подбор оборудования выполняет проектная организация; лист задаёт места и высоты выводов.


					Проект: Квартира 65 м²	М 1:20
	Лист	№ док.	Подпись	Дата	Развёртки мокрых зон: выводы ВК. Ванная (лист 1 из 2)	
Дизайнер	Кырлан А.С.			04.11.26		

Стадия	Лист	Листов
П	22	83

Стена В (М 1:20)

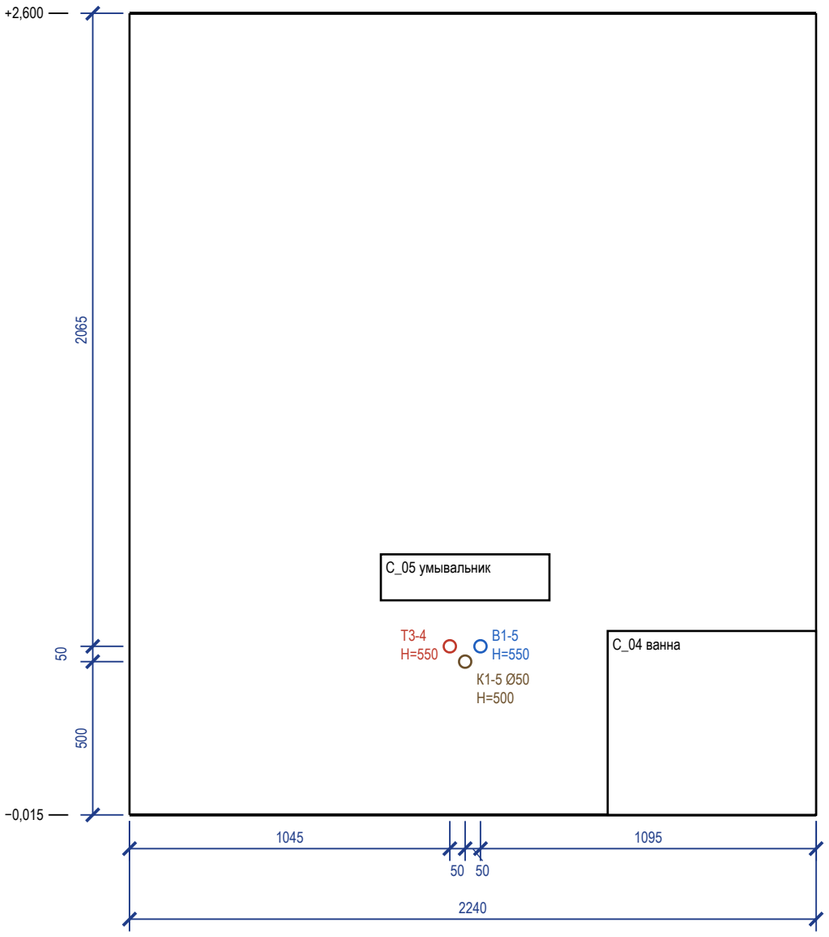

Стена Г (М 1:20)

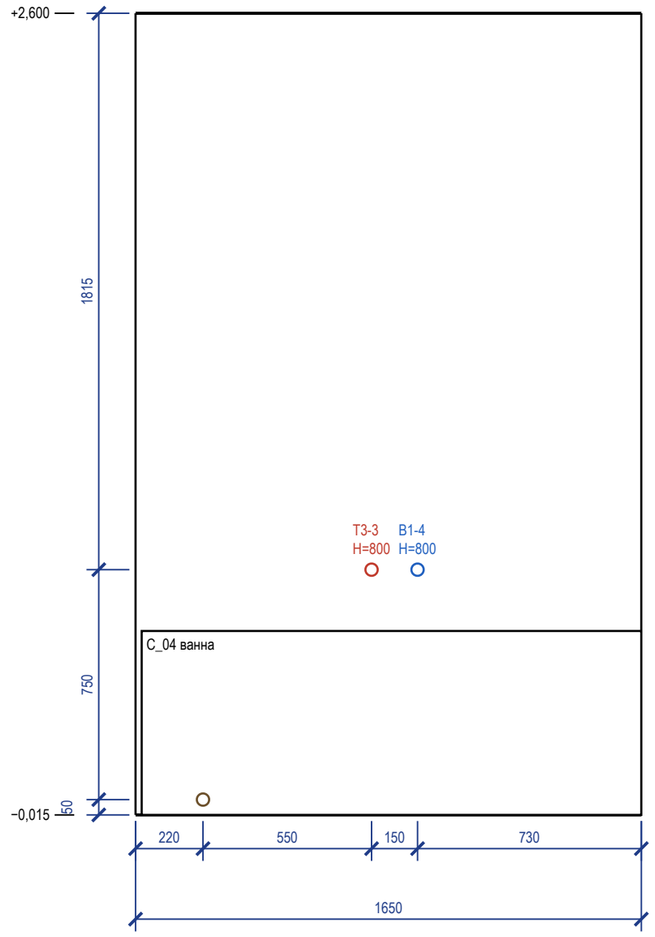

Ведомость привязок выводов (от чистого пола и угла)

Код	Прибор	Ø	H, мм	Привязка, мм
B1-5	C_05 умывальник	½"	550	ст. В: 1145 от лев. угла
T3-4	C_05 умывальник	½"	550	ст. В: 1045 от лев. угла
K1-5	C_05 умывальник	Ø50	500	ст. В: 1095 от лев. угла
B1-4	C_04 ванна	½"	800	ст. Г: 920 от лев. угла
T3-3	C_04 ванна	½"	800	ст. Г: 770 от лев. угла
K1-4	C_04 ванна	Ø50	50	ст. Г: 220 от лев. угла

Условные обозначения

- вывод B1 (код — в ведомости привязок)
- вывод T3 (код — в ведомости привязок)
- вывод K1 (код — в ведомости привязок)
- сантехприбор по расстановке (габарит модели)
- дверной проём; окно — сплошной контур

Примечания

1. Габариты и высоты приборов, межосевые смесителей и места кранов — по паспортам выбранных приборов, сверяются до разметки стен.
2. Высоты H — от чистого пола помещения, мм; отметка чистого пола и потолка — у левого края вида (от ±0,000 объекта). Привязки — от левого чистового угла вида (облицовка стен вычтена), как на развёртках стен.
3. Ревизионные люки (арматура и ревизии у C_04 300×400, стена Г у C_04, предложение): привязка к углу — по раскладке плитки, подтверждается обмером.
4. Ревизионные люки к арматуре и ревизиям в данных не заданы: место и размер не определены (записи реестра нет).
5. Часть подписей выводов не уместилась у знака: коды и высоты — в ведомости привязок.
6. Помещение «Ванная» — 2 листа: стены 1) А, Б; 2) В, Г.
7. Расчёт систем водоснабжения и канализации и подбор оборудования выполняет проектная организация; лист задаёт места и высоты выводов.

					Проект: Квартира 65 м²	М 1:20
	Лист	№ док.	Подпись	Дата	Развёртки мокрых зон: выводы ВК. Ванная (лист 2 из 2)	
Дизайнер	Кырлан А.С.			04.11.26		

Стадия	Лист	Листов
П	23	83


выпуск 04.11.2026 № 84932ed378 · стр. 23 из 83

Поз.	Наименование и техническая характеристика	Тип, марка, обозначение документа	Код продукции	Поставщик	Ед. изм.	Кол.	Масса 1 ед., кг	Примечание
	Санитарные приборы							
1	Ванна встраиваемая акриловая 1650×700 мм, с каркасом, экраном и отверстием слив-перелив	Ravak Classic C541000000		выбор заказчика	шт	1		С_04
2	Унитаз подвесной безободковый, с сиденьем микролифт, крепёж и звукоизолирующая прокладка	Jacob Delafon Struktura EDF102-00		выбор заказчика	шт	1		С_02
3	Инсталляция для подвесного унитаза: рама высотой 1120 мм, бачок, клавиша смыва (ось клавиши 1050 мм от чистого пола)	аналог		выбор заказчика	шт	1		С_02; короб ГКЛВ
4	Умывальник подвесной 400×300 мм, с отверстием под смеситель и переливом	Roca The Gap 7.3274.7.400.0		выбор заказчика	шт	1		С_03
5	Умывальник подвесной 550×450 мм, с отверстием под смеситель и переливом	Roca The Gap 7.3274.7.400.0		выбор заказчика	шт	1		С_05
6	Мойка кухонная 700×480 мм, с переливом	мойка врезная 700×480 в шкафу М_11		с кухонной мебелью	шт	1		С_01
7	Полотенцесушитель электрический, IP44, с терморегулятором	аналог		выбор заказчика	шт	1		С_06
	Смесители, сифоны и арматура приборов							
8	Смеситель для ванны настенный однорычажный, межосевое 150 мм, с душевым набором (лейка, шланг, держатель)	аналог		выбор заказчика	шт	1		С_04
9	Смеситель для умывальника однорычажный, с донным клапаном	аналог		выбор заказчика	шт	2		С_03, С_05
10	Смеситель кухонный однорычажный, высокий излив	аналог		выбор заказчика	шт	1		С_01
11	Обвязка ванны слив-перелив Ø40/50 с сифоном	аналог		выбор заказчика	шт	1		С_04
12	Сифон для умывальника бутылочный Ø32/40–50, с гофрой к выпуску	аналог		выбор заказчика	шт	2		С_03, С_05
13	Сифон для мойки Ø40/50	аналог		выбор заказчика	шт	1		С_01
14	Сифон для стиральной машины встраиваемый в стену Ø50, с обратным клапаном	аналог		выбор заказчика	шт	1		ОБ_02
15	Кран угловой ½"×½" с гибкой подводкой 40 см (умывальники, мойка)	аналог		выбор заказчика	шт	6		по 2 на прибор
16	Кран шаровой угловой ½"×¾" для подключения стиральной и посудомоечной машины	аналог		выбор заказчика	шт	1		ОБ_02
	Трубопроводы							
17	Труба полипропиленовая PP-R PN20 Ø20×3,4 (В1)	ГОСТ 32415-2013		выбор заказчика	м	17	0,17	10,9 + 4,3 + 10 %
18	Труба PP-R, армированная стекловолокном, PN20 Ø20×2,8 (Т3)	ГОСТ 32415-2013		выбор заказчика	м	12	0,15	8,4 + 2,5 + 10 %
19	Труба канализационная ПП Ø50 (К1)	ГОСТ 32414-2013		выбор заказчика	м	13		9,6 + 2,0 + 10 %
20	Труба канализационная ПП Ø110 (К1)	ГОСТ 32414-2013		выбор заказчика	м	1,5		0,8 + 0,2 + 10 %
	Фасонные части и выводы							
21	Отвод канализационный ПП 45° Ø50	ГОСТ 32414-2013		выбор заказчика	шт	20		2 шт. на поворот
22	Отвод канализационный ПП 45° Ø110	ГОСТ 32414-2013		выбор заказчика	шт	6		2 шт. на поворот
23	Тройник канализационный ПП 45° (врезки ветвей)	ГОСТ 32414-2013		выбор заказчика	шт	5		
24	Ревизия канализационная ПП (после поворота трассы)	ГОСТ 32414-2013		выбор заказчика	шт	8		доступ сохранить
25	Фитинги PP-R Ø20: тройники, угольники 90° (ветви и повороты В1, Т3)	ГОСТ 32415-2013		выбор заказчика	шт	29		
26	Водорозетка PP-R Ø20×½" настенная, с креплением	ГОСТ 32415-2013		выбор заказчика	шт	10		коды — лист выводов
	Узлы ввода, люки, короба							
27	Кран шаровой латунный Ду15 PN16 (отключение ввода)	аналог		выбор заказчика	шт	2		Ст В1-1, Ст Т3-1
28	Фильтр сетчатый косой Ду15	аналог		выбор заказчика	шт	2		
29	Счётчик воды крыльчатый Ду15 (ХВ, ГВ), с поверкой	аналог		выбор заказчика	шт	2		пломба УК
30	Клапан обратный Ду15	аналог		выбор заказчика	шт	2		
31	Люк ревизионный нажимной под плитку 300×400 мм	аналог		выбор заказчика	шт	3		к стоякам и арматуре
32	Звукоизоляция стояка К1 в коробе: рулонный звукоизоляционный материал ≥ 10 мм, обмотка стояка на высоту этажа	аналог		выбор заказчика	м	2,7		Ст К1-1
33	Короб К1 над полом: профиль ПН/ПС, ГКЛВ 12,5 мм под плитку	аналог		выбор заказчика	м	2,9		сечение — лист разводки

Примечания

1. Форма 1 ГОСТ 21.110-2013, ширины граф изменены по п. 4.1. «Аналог» — аналог по характеристикам: модели внести до черновых работ, привязки выводов сверить по паспортам.
2. Бытовая техника не входит (показана арматура подключения), мойка — в комплекте кухни (марка — модуля кухни, как у столяра). Длины труб — трасса листа разводки + подъёмы + 10 %.
3. Стояк К1 в коробе — звукоизоляция стояка в коробе без жёсткого контакта короба с трубой.
4. Расчёт систем водоснабжения и канализации, диаметры магистралей и подбор оборудования выполняет проектная организация.

					Проект: Квартира 65 м²		
	Лист	№ док.	Подпись	Дата	Спецификация сантехнического оборудования	Стадия	Лист	Листов
Дизайнер	Кырлан А.С.			04.11.26		П	24	83

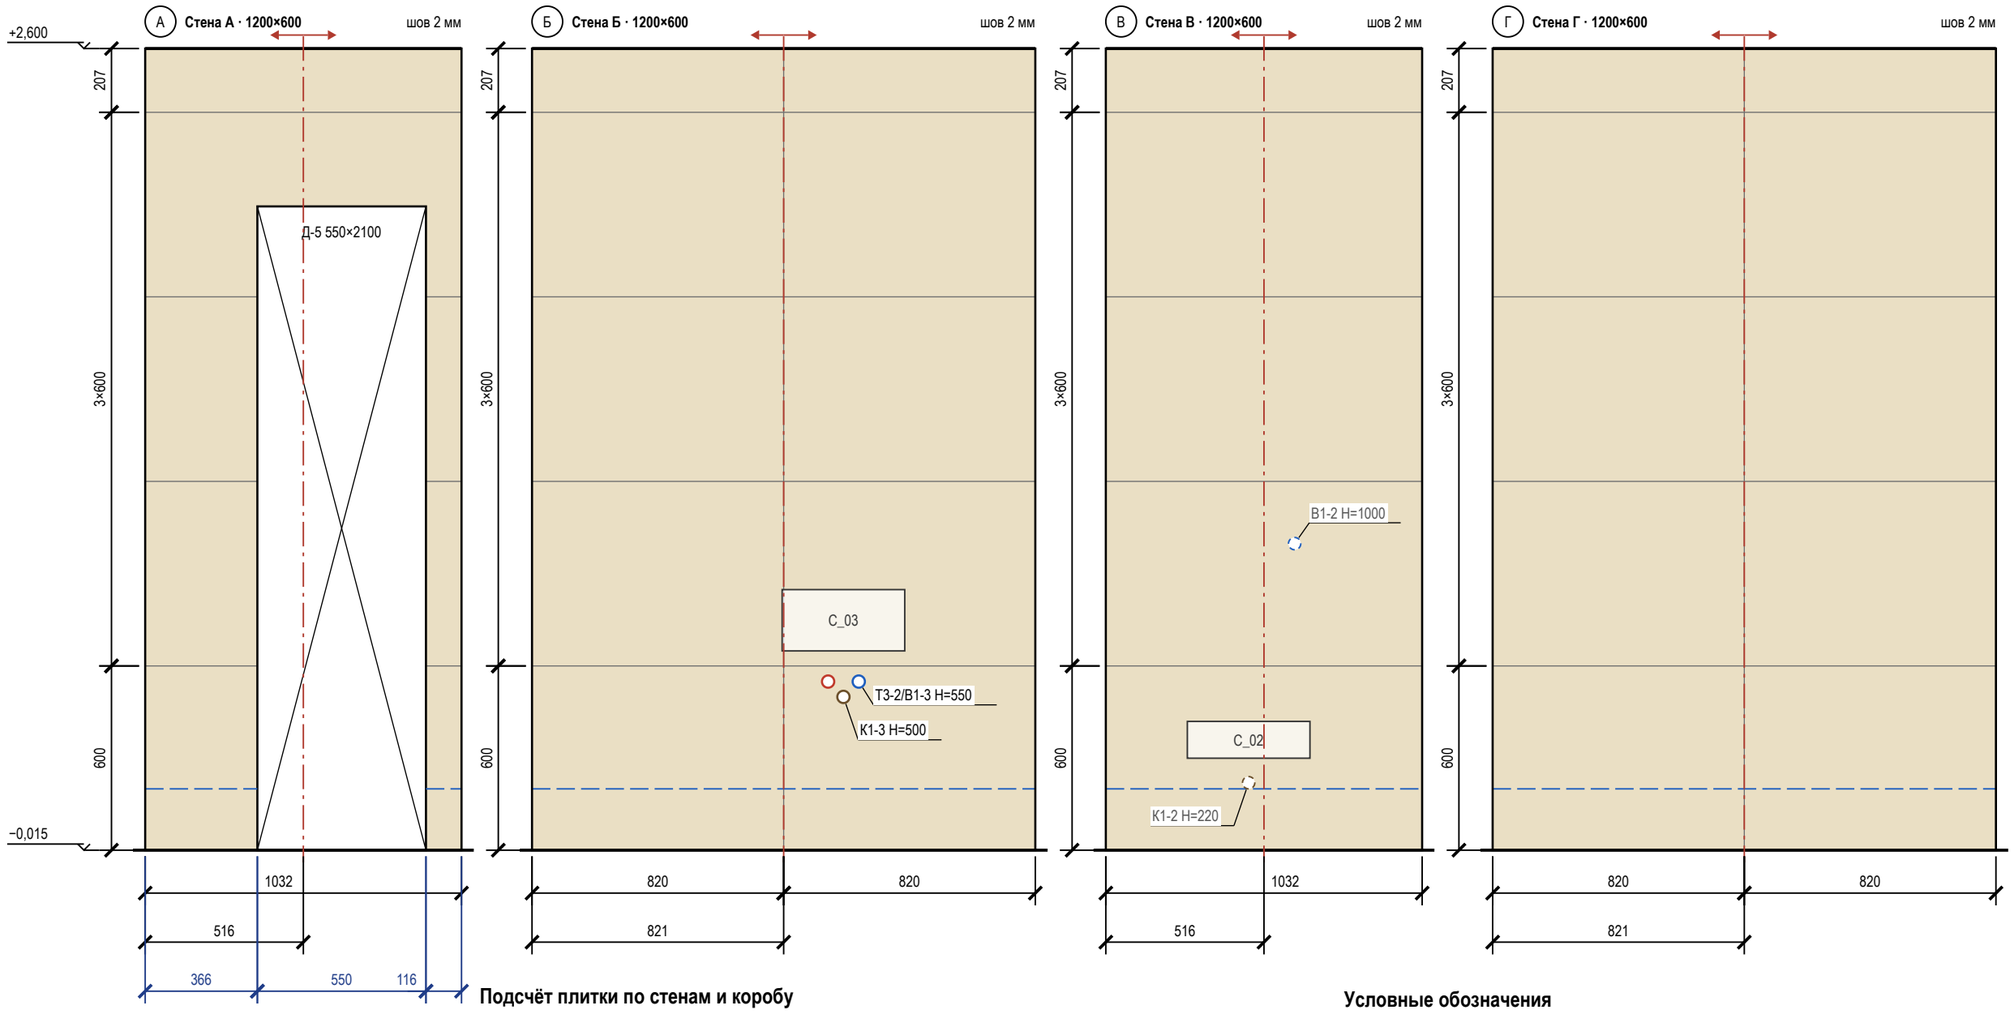

Подсчёт плитки по стенам и коробу

Поверхность	L × H, мм	S, м²	Целых	Подр.	С запасом	Подрезки: край / верх, мм
стена А	1032 × 2615	1,67	0	5	6	1032; 207
стена Б	1642 × 2615	4,42	0	10	11	820 / 820; 207
стена В	1032 × 2615	2,82	0	5	6	1032; 207
стена Г	1642 × 2615	4,42	0	10	11	820 / 820; 207
Итого		**13,33**	**0**	**30**	**34**	

Условные обозначения

- плитка целая; тонкая линия — шов
- плитка с подрезкой (размер — на цепочке)
- ось старта; стрелки — направление укладки
- верх гидроизоляции: 200 от ЧП, в мокрой зоне — «до …»
- проём — не облицовывается
- сантехприбор: габарит, высота по практике
- вывод B1 (код — в ведомости привязок)
- вывод T3 (код — в ведомости привязок)
- вывод K1 (код — в ведомости привязок)
- вывод за прибором / в коробе (не на сетке)
- отметка уровня, м: ±0,000 — чистый пол жилых помещений
- низ потолка; серая полоса — стена без плитки
- (А) обозначение стены А–Г (как на развёртках)

Примечания

1. Вид изнутри, стены по часовой стрелке А → Г. Высоты — от чистого пола (−0,015), отметки — от ±0,000. Раскладка от чистовых размеров (штукатурка 10 + клей 5 + плитка 9 мм), подрезки чистые; старт — от оси стены, ряды от пола целыми.
2. Облицовка до потолка (+2,600).
3. Открытые выводы и электроточки — на шве или в центре плитки (допуск 10 мм; плитка от 900 мм по высоте — на шве или не ближе 60 мм к нему).
4. Выводы ВК стоят по оси прибора и с прибором не двигаются — привязки по «Плану выводов сантехники» без сдвига; вне сетки (T3-2/B1-3, K1-3) — отверстие в плитке коронкой по той же привязке, плитку не сдвигать.
5. За приборами и в коробе (B1-2, K1-2) — штриховым кольцом.
6. Гидроизоляция: 200 мм от ЧП по периметру; углы — лентой; акт скрытых работ, пролив.


	Лист	№ док.	Подпись	Дата
Дизайнер	Кырлан А.С.			04.11.26

Проект: Квартира 65 м² — **М 1:20**

Раскладка плитки. Санузел. Развёртки стен

Стадия	Лист	Листов
П	25	83

выпуск 04.11.2026 № 84932ed378 · стр. 25 из 83

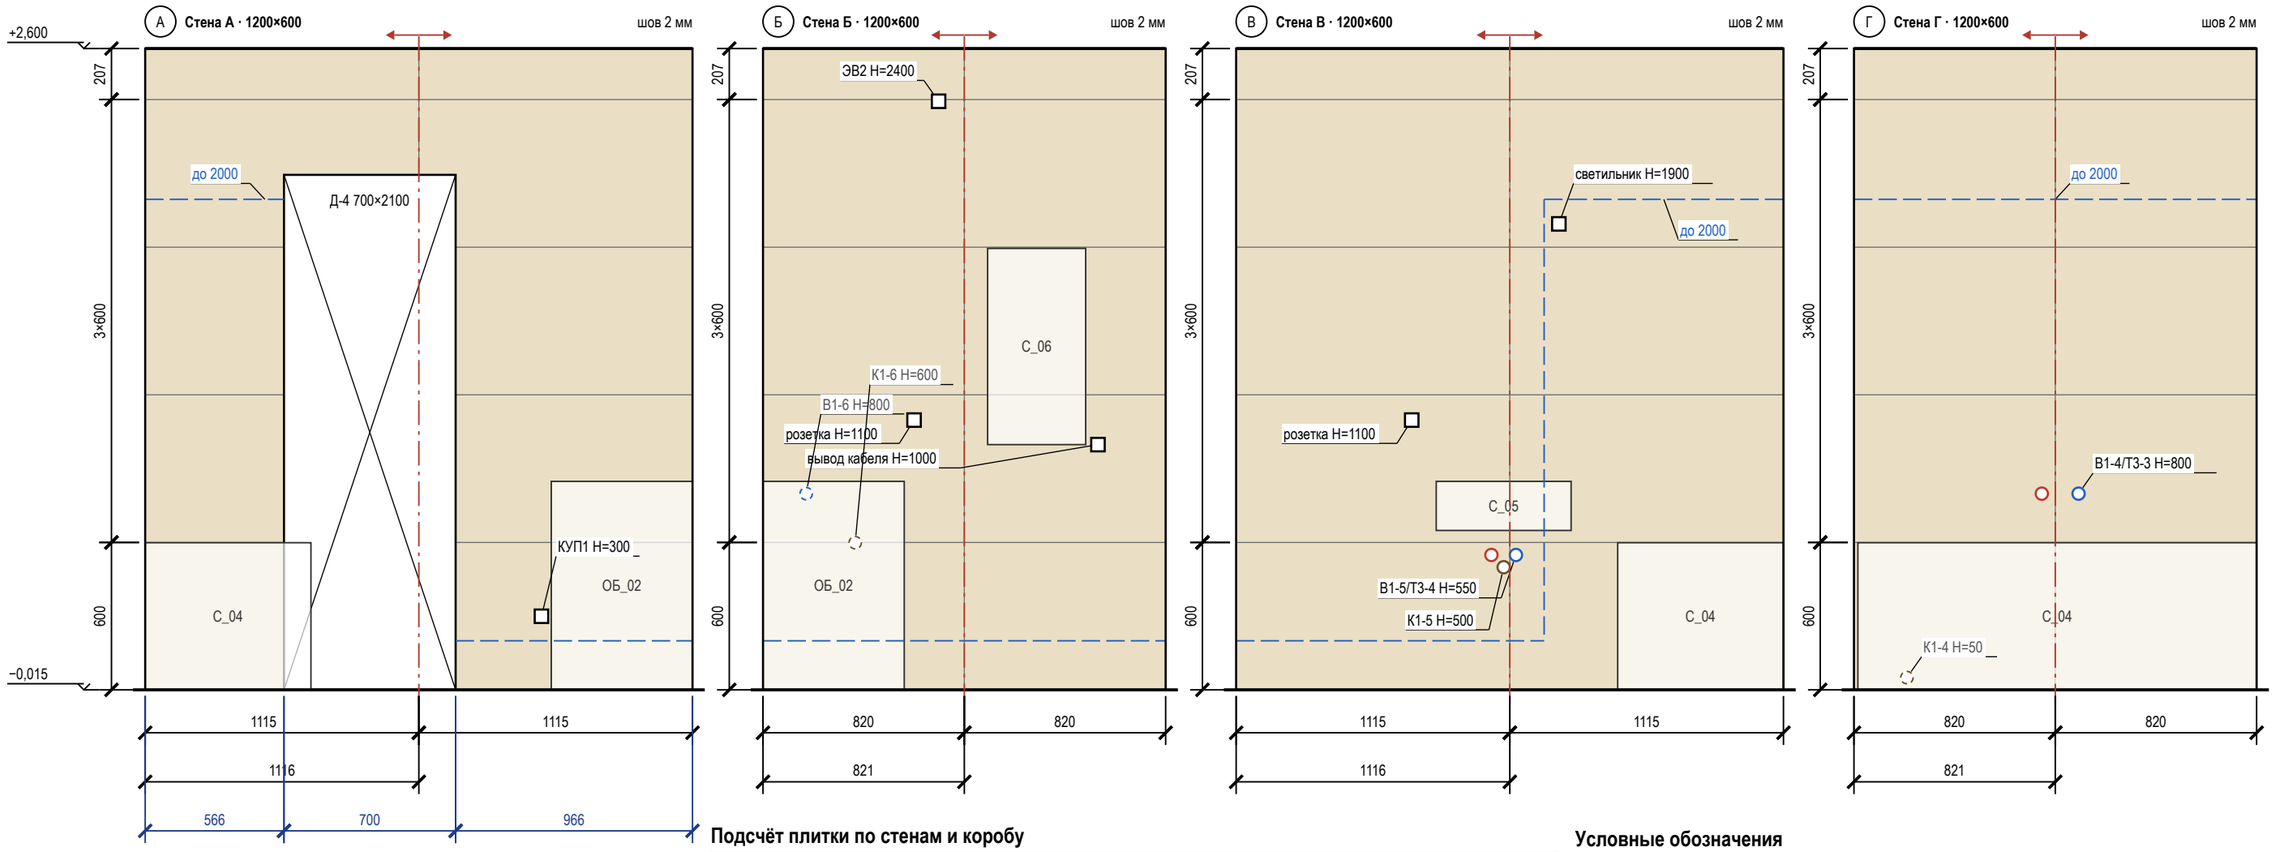

Подсчёт плитки по стенам и коробу

Поверхность	L × H, мм	S, м²	Целых	Подр.	С запасом	Подрезки: край / верх, мм
стена А	2232 × 2615	4,49	0	10	11	1115 / 1115; 207
стена Б	1642 × 2615	4,42	0	10	11	820 / 820; 207
стена В	2232 × 2615	5,96	0	10	11	1115 / 1115; 207
стена Г	1642 × 2615	4,42	0	10	11	820 / 820; 207
Итого		**19,29**	**0**	**40**	**44**	

Сдвиг точек под раскладку

Точка (ВК, ЭОМ)	Стена	Проект: от угла / H	Под раскладку: от угла / H	Сдвиг, мм
вывод кабеля	Б	1366 / 1000	1366 / 902	H −98
розетка	Б	616 / 1100	616 / 1203	H +103
розетка	В	716 / 1100	716 / 1203	H +103
светильник	В	1316 / 1900	1316 / 1805	H −95

Условные обозначения


- плитка целая; тонкая линия — шов
- плитка с подрезкой (размер — на цепочке)
- ось старта; стрелки — направление укладки
- верх гидроизоляции: 200 от ЧП, в мокрой зоне — «до …»
- проём — не облицовывается
- сантехприбор: габарит, высота по практике
- вывод В1 (код — в ведомости привязок)
- вывод Т3 (код — в ведомости привязок)
- вывод К1 (код — в ведомости привязок)
- вывод за прибором / в коробе (не на сетке)
- электроточка: марка и H — по листам ЭОМ
- отметка уровня, м: ±0,000 — чистый пол жилых помещений
- низ потолка; серая полоса — стена без плитки
- (А) обозначение стены А–Г (как на развёртках)

Примечания

1. Вид изнутри, стены по часовой стрелке А → Г. Высоты — от чистого пола (−0,015), отметки — от ±0,000. Раскладка от чистовых размеров (штукатурка 10 + клей 5 + плитка 9 мм), подрезки чистые; старт — от оси стены, ряды от пола целыми.
2. Облицовка до потолка (+2,600).
3. Точки из таблицы сдвигов переносятся до черновой разводки (ЭОМ — по тем же числам).
4. Выводы ВК стоят по оси прибора и с прибором не двигаются — привязки по «Плану выводов сантехники» без сдвига; вне сетки (В1-5/Т3-4, К1-5, В1-4/Т3-3) отверстие в плитке коронкой по той же привязке, плитку не сдвигать.
5. За приборами и в коробе (В1-6, К1-6, К1-4) — штриховым кольцом.
6. Гидроизоляция: 200 мм от ЧП по периметру; над ванной — до 2000 и 300 мм за борт (СП 29.13330.2011, п. 7.2 — на высоту замачивания); углы — лентой; акт скрытых работ, пролив.

					Проект: Квартира 65 м²	М 1:25
	Лист	№ док.	Подпись	Дата		
Дизайнер	Кырлан А.С.			04.11.26	Раскладка плитки. Ванная. Развёртки стен	Стадия: П; Лист: 26; Листов: 83

выпуск 04.11.2026 № 84932ed378 · стр. 26 из 83

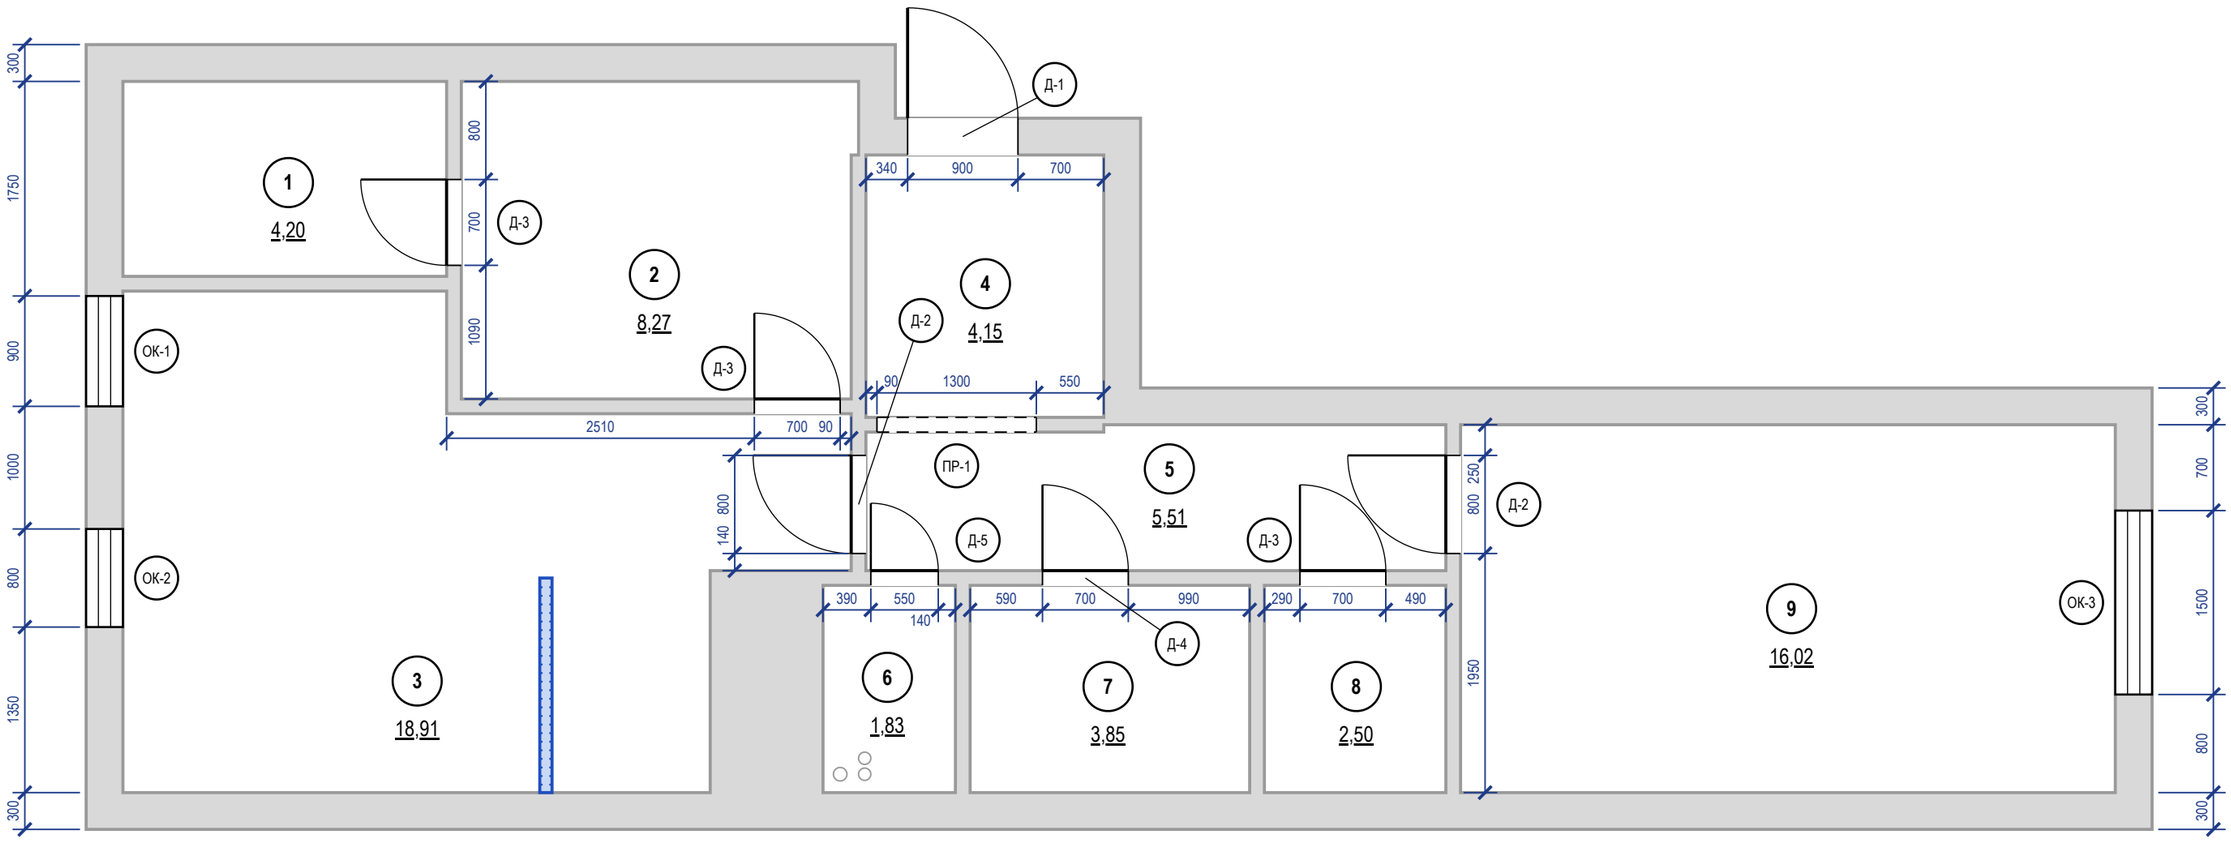

Ведомость заполнения проёмов


Марка	Наименование, обозначение	Проём ш×в, мм	Полотно (расч.)	Кол.	Откр.	Отделка полотна	Фурнитура	Прим.
Д-1	Блок дверной входной, ГОСТ 31173-2016	900×2100	блок задать	1	П	в комплекте блока	в комплекте блока (замки, глазок)	наружу
Д-2	Дверь скрытого монтажа, Profil Doors Invisible	800×2100	700×2050	2	Л, Л	S 1002-Y50R — пом. 3, S 1502-Y50R — пом. 5; S 1502-Y50R — пом. 5, No. 241 — пом. 9	скрытые петли 3D, магнитный замок	
Д-3	Дверь скрытого монтажа, Profil Doors Invisible	700×2100	600×2050	3	Л, П, П	V503 — пом. 1, S 1502-Y50R — пом. 2; S 1502-Y50R — пом. 2, S 1002-Y50R — пом. 3; S 1502-Y50R — пом. 5, S 0502-Y — пом. 8	скрытые петли 3D, магнитный замок	
Д-4	Дверь скрытого монтажа, Profil Doors Invisible	700×2100	600×2050	1	П	S 1502-Y50R — пом. 5, в тон облицовки — пом. 7	скрытые петли 3D, магнитный замок, фиксатор WC	порог 15
Д-5	Дверь скрытого монтажа, Profil Doors Invisible	550×2100	450×2050	1	П	S 1502-Y50R — пом. 5, в тон облицовки — пом. 6	скрытые петли 3D, магнитный замок, фиксатор WC	порог 15
ПР-1	Портал без заполнения	1300×2100		1				б/п
ОК-1	Блок оконный, ГОСТ 23166-2021	900×1600		1				низ 800
ОК-2	Блок оконный, ГОСТ 23166-2021	800×1600		1				низ 800
ОК-3	Блок оконный, ГОСТ 23166-2021	1500×1600		1				низ 800

Примечания

1. Размеры проёмов и привязки — в миллиметрах от чистых граней стен до отделки; привязка — от угла того помещения, со стороны которого стоит размер. Размер проёма — ширина × высота от чистого пола 0,000. Размеры на плане — проёмов, не полотен: полотно — в ведомости, коробка — по системе. Откос от угла помещения до проёма с коробкой — не менее 50 мм.
2. Марки в кружках — типы заполнения проёмов (ГОСТ 21.501-2018, п. 5.3.2); одна марка — один типоразмер; количество сверено с планом.
3. Открывание: Л — петли слева, П — справа, если смотреть со стороны, куда открывается полотно (на себя).
4. Скрытые двери (Д-2…Д-5): проём замерить в чистоте; блок заказать до штукатурки (≈ 30 дн.), короб ставить до штукатурки; полотно навесить после чистовой отделки, красить в цвет стен. Порядок практика монтажа, изготовитель подтверждает.
5. Д-2…Д-5 — существующие проёмы, до техзаключения не расширять.
6. Полотно «расч.» — по проёму и ряду изделия с запасом по каталогам, заказ — по таблице проёмов модели; Д-1: входной блок по ГОСТ 31173-2016 — задать при выборе блока.
7. Размеры проёмов и привязки сняты со скана плана заказчика и на объекте не замерены (обмерный план — лист 5).
8. Экспликация помещений — лист 5; в марках помещений — номер и площадь, м².

					Проект: Квартира 65 м²	**М 1:50**
	Лист	№ док.	Подпись	Дата	План размещения дверей	Стадия / Лист / Листов
Дизайнер	Кырлан А.С.			04.11.26		П / 27 / 83

выпуск 04.11.2026 № 84932ed378 · стр. 27 из 83

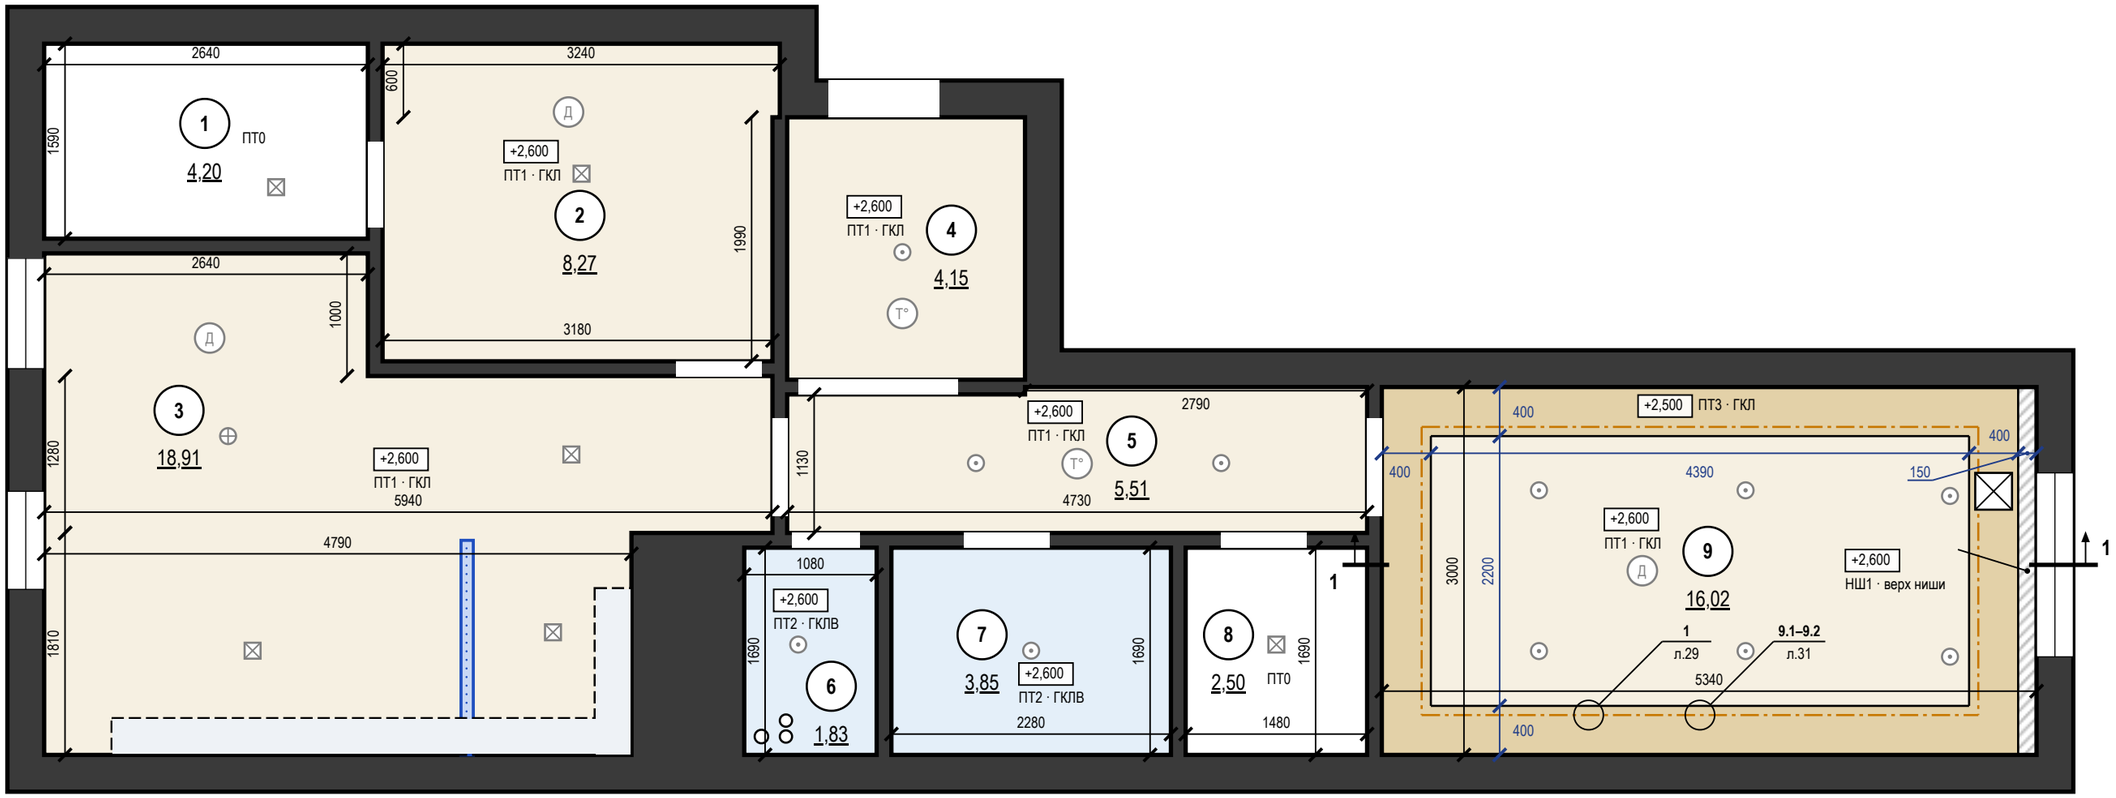

Ведомость потолков

Пом.	Марка	Конструкция	Низ / верх ниши	S, м²	Q
1, 8	ПТ0	Существующий потолок, окраска	+2,700	6,70	
2	ПТ1	ГКЛ П113	+2,600	8,27	Q3
3	ПТ1	То же	+2,600	18,91	Q3
4	ПТ1	То же	+2,600	4,15	Q3
5	ПТ1	То же	+2,600	5,51	Q3
6	ПТ2	ГКЛВ П113	+2,600	1,83	Q3
7	ПТ2	То же	+2,600	3,85	Q3
9	ПТ3	ГКЛ П113, короб LED	+2,500	5,91	Q3
9	ПТ1	ГКЛ П113	+2,600	9,66	Q3
9	НШ1	ниша под шторы 150×100	+2,600	0,45	
		Итого		**65,24**	

Ведомость вырезов и закладных в потолке

Марка	Устройство	Кол.	Пом.
	Светильник встраиваемый (марки — план освещения)	11	4, 5, 6, 7, 9
	Светильник накладной (марки — план освещения)	6	1, 2, 3, 8
	Светильник подвесной (марки — план освещения)	1	3
ИП2	Извещатель дымовой	3	2, 3, 9
ИП3, ИП4	Извещатель тепловой	2	4, 5
	Люк ревизии 300×300	1	9

Примечания

1. За отметку ±0,000 принят уровень чистого пола сухих помещений (готовое покрытие), а не существующего пола; пол пом. 6, 7 — −0,015; верх плиты перекрытия −0,064 — расчётный по пирогу пола, не замерен; существующий пол снимается до плиты, его отметка не замерена. Отметки в прямоугольниках — низ потолка; низ перекрытия +2,700. Марка потолка — одна конструкция и отметка на весь альбом.
2. Размеры помещений в свету (ширина × длина, мм), не поместившиеся на плане: пом. 4 — 1940 × 2140.
3. Потолки ГКЛ — каркасная система П113: подвесы через 1000 (с запасом: СП 163, табл. 14 — до 1100 при 0,15 кН/м²), несущие профили через 500, основные через 1200 мм; листы — поперёк несущих профилей. В помещениях 6, 7 — ГКЛВ на оцинкованном каркасе.
4. Нижний уровень — пояс-короб по периметру шириной 400 мм, верхний — поле внутри пояса: пом. 9.
5. LED-лента в алюминиевом профиле посередине карниза короба шириной 400 мм (узел 1, лист 29); длина по плану: пом. 9 — 13,8 м (в плане освещения 13,8).
6. Ниши под шторы 150×100 мм — на всю длину стены с окном; карниз — на закладной до обшивки (узел 2, лист 29).
7. Примыкание к стенам: теневой шов 15 мм, техзазор 3 мм — пом. 2, 3, 4, 5, 9, по стенам, выровненным штукатуркой (узел 1); пом. 6, 7 — разделительная лента.
8. Светильники и потолочные устройства — подложка с планов освещения, слаботочных систем и вентиляции (положение — по ним); вырезы и закладные — по ведомости на листе, до обшивки; отверстия не совмещать с профилями, глубина корпуса светильника до 70 мм.
9. Разрезы 1–1 — на листе 29; высоты мебели и дверных блоков сверены с низом потолка в разрезах.
10. Шпаклевание ГКЛ и условия приёмки — Q3: рассеянный дневной свет, осмотр с 2 м; боковой свет не оценивается.
11. Пом. 3: короб воздуховода кухонной вытяжки ГКЛ 300×200 мм (ширина от стены × высота), низ +2,500, длина 5,00 м — по трассе плана вентиляции, вдоль стен до входа в канал под воздуховод Ø125; каркас ПН 28×27 по стене и плите, ПП 60×27, лист ГКЛ 12,5.
12. Люки ревизии 300×300 мм — по центру блоков питания LED (БП3; координаты — план освещения).
13. ПТ0 — пом. 1, 8: существующий потолок, окраска, без подвесного потолка, низ +2,700; материал и цвет — по ведомости отделки.

	Лист	№ док.	Подпись	Дата
Дизайнер	Кырлан А.С.			04.11.26


Проект: Квартира 65 м² — **М 1:50**

План потолков

Стадия	Лист	Листов
П	28	83


Разрез 1–1 (М 1:40)

Пом. 9 Детская; линия разреза — план потолков, лист 28

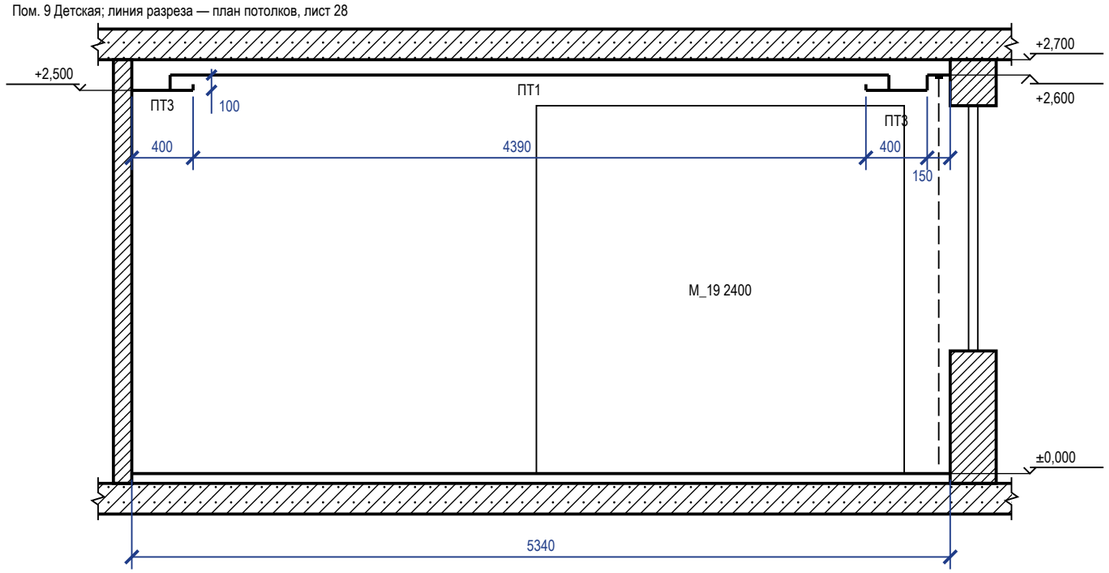

1 Короб с LED-подсветкой, теневой шов (М 1:10)


Пом. 9; карниз 150×100, щель под свет 60 мм

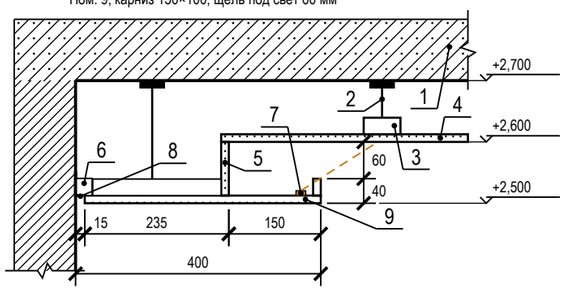

1 — плита перекрытия
2 — подвес прямой, шаг 1000 мм
3 — ПП 60×27: несущие через 500, основные через 1200 мм
4 — ГКЛ 12,5 по П113 — верхний уровень
5 — задняя стенка и бортик карниза — ГКЛ 12,5
6 — ПН 28×27 по периметру, к стене через 500 мм
7 — LED-лента в алюминиевом профиле
8 — теневой профиль: шов 15 мм, зазор 3 мм
9 — низ короба — ГКЛ 12,5 по ПП 60×27

2 Ниша под шторы (М 1:10)

Пом. 9; без подсветки; закладные под карниз — до обшивки

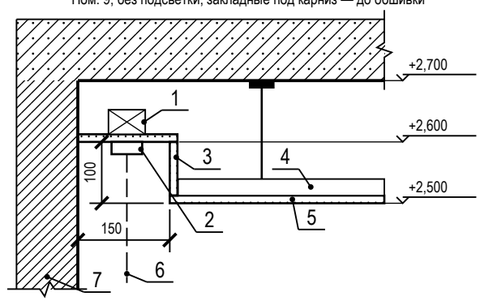

1 — закладная под карниз — брус 40×50
2 — карниз (шина), высота с верхом портьеры 80 мм
3 — стенка и потолок ниши — ГКЛ 12,5
4 — ПП 60×27 — каркас короба
5 — низ короба нижнего уровня — ГКЛ 12,5
6 — портьера
7 — стена с окном

Условные обозначения

- плита перекрытия в сечении
- стена в сечении
- потолок ГКЛ в сечении; под линией — марка потолка (план потолков)
- мебель и дверные проёмы за секущей плоскостью; число — марка и верх от чистого пола, мм
- портьера в нише под шторы

Примечания

1. Разрезы — по линиям 1–1 на плане потолков (лист 28). Отметки — от ±0,000 чистого пола, м; размеры — мм.
2. Высоты мебели и дверных блоков за секущей плоскостью сверены с низом потолка над ними: верх ниже низа короба и поля.
3. ГКЛ 12,5 мм по каркасу П113; перепад уровней и бортик карниза — ГКЛ по ПП 60×27 (узел 1 — на этом листе). Ниша под шторы — на всю длину стены с окном, карниз на закладной до обшивки (узел 2 — на этом листе).
4. Толщины плит перекрытия и пирога пола показаны условно.
5. Сечения потолков по помещениям М 1:10 (отметки помещения, профили, подвесы, крепёж, изделия) — лист 31.
6. Ведомость объёмов потолков (лист ГКЛ, профиль, подвесы, лента, блоки питания, люки) — на листе 30.

					Проект: Квартира 65 м²	М 1:40; 1:10
	Лист	№ док.	Подпись	Дата		
Дизайнер	Кырлан А.С.			04.11.26	Разрезы и узлы потолков	Стадия: П; Лист: 29; Листов: 83

Ведомость объёмов потолков

Позиция	Ед.	Кол.	Пом.
Лист ГКЛ 12,5	м²	57,10	2, 3, 4, 5, 9
Лист ГКЛВ 12,5	м²	5,68	6, 7
Борта и карнизы (входят в площади листов выше)	м²	4,24	9
Профиль ПП 60×27	м	169,79	2, 3, 4, 5, 6, 7, 9
Профиль ПН 28×27	м	128,02	2, 3, 4, 5, 6, 7, 9
Подвес прямой	шт.	64	2, 3, 4, 5, 6, 7, 9
Анкер-клин к плите	шт.	64	2, 3, 4, 5, 6, 7, 9
Шуруп TN 3,5×25	шт.	1444	2, 3, 4, 5, 6, 7, 9
Лента армирующая для швов	м	75,34	2, 3, 4, 5, 6, 7, 9
Шпаклёвка для швов	кг	25,11	2, 3, 4, 5, 6, 7, 9
Грунтовка (швы)	л	6,28	2, 3, 4, 5, 6, 7, 9
Лента разделительная по периметру	м	81,88	2, 3, 4, 5, 6, 7, 9
Сплошная шпаклёвка и окраска (площадь развёртки)	м²	62,78	2, 3, 4, 5, 6, 7, 9
Лента LED	м	13,78	9
Требуемая мощность блоков питания	Вт	172	9
Установленная мощность блоков питания	Вт	200	9
Блок питания LED	шт.	1	9
Люк ревизии	шт.	1	9


Примечания

1. ГКЛ 12,5 мм по каркасу П113; узлы коробов и ниш под шторы: узел 1 — лист 29; узел 2 — лист 29; условные обозначения разрезов — на листе 29.
2. Ведомость объёмов — по геометрии плана потолков: Лист ГКЛ 12,5 — плоскости уровней + борта (без арочных участков); Лист ГКЛВ 12,5 — плоскости уровней + борта; Борта и карнизы — длина перепада × перепад; Профиль ПП 60×27 — S × (1/шаг несущ. + 1/шаг осн.) + стойки бортов; Профиль ПН 28×27 — периметр стен + 2 × перепады + карнизы; Подвес прямой — по раскладке: S уровня / (шаг осн. × шаг подвесов), пояс уже шага — ряд вдоль пояса, фигура — по контуру; шаг подвесов — не больше табл. 14 СП 163; Анкер-клин к плите — по одному на подвес (Knauf П113); Шуруп TN 3,5×25 — 23 шт./м² (Knauf П113, табл. 2 альбома П 11); Лента армирующая для швов — 1,2 м/м² листа (Knauf); Шпаклёвка для швов — 0,4 кг/м² листа, только швы (Knauf); Грунтовка (швы) — 0,1 л/м² листа, только швы (Knauf); Лента разделительная по периметру — периметр стен под потолком ГКЛ; Сплошная шпаклёвка и окраска (площадь развёртки) — плоскости + борта; расход — по паспорту материала (норма расхода на сплошной слой не подтверждена); Лента LED — по оси карниза и ниши фигуры (план потолков); Требуемая мощность блоков питания — Вт/м × длина × 1,3; Установленная мощность блоков питания — сумма мощностей блоков по плану освещения; Блок питания LED — блоки потолочных лент по плану освещения (БП3); Люк ревизии — план потолков; без запаса на подрезку (при закупке листа: ×1,075 при S > 20 м², ×1,175 — 10–20 м², ×1,275 — < 10 м²).

					Проект: Квартира 65 м²
	Лист	№ док.	Подпись	Дата	
Дизайнер	Кырлан А.С.			04.11.26	Разрезы и узлы потолков (продолжение)
					Стадия: П; Лист: 30; Листов: 83

Сечение 9.1. Короб с LED-подсветкой, теневой шов (М 1:10)


Пом. 9 Детская; карниз 150×100, щель под свет 60 мм

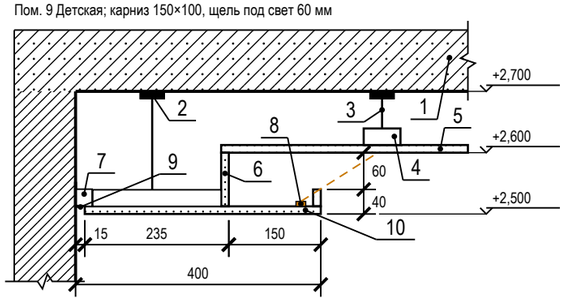

1 — плита перекрытия
2 — анкер-клин к плите — по одному на подвес
3 — подвес прямой, шаг 1000 мм
4 — ПП 60×27: несущие через 500, основные через 1200 мм; соединители одноуровневые, шурупы LN 3,5×9
5 — ГКЛ 12,5 по П113 — верхний уровень; шурупы TN 3,5×25 через 170 мм
6 — задняя стенка и бортик карниза — ГКЛ 12,5
7 — ПН 28×27 по периметру — дюбель-гвоздь через ≤ 500 мм, не менее 3 на профиль
8 — LED-лента 9,6 Вт/м, 24 В в алюминиевом профиле
9 — теневой профиль: шов 15 мм, зазор 3 мм
10 — низ короба — ГКЛ 12,5 по ПП 60×27

Сечение 9.2. Ниша под шторы (М 1:10)

Пом. 9 Детская; без подсветки; закладные под карниз — до обшивки

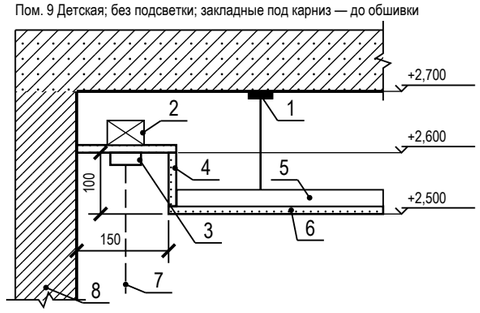

1 — анкер-клин к плите — по одному на подвес; подвес прямой, шаг 1000 мм
2 — закладная под карниз — брус 40×50
3 — карниз (шина), высота с верхом портьеры 80 мм
4 — стенка и потолок ниши — ГКЛ 12,5
5 — ПП 60×27 — каркас короба, основные через 1200 мм; соединители одноуровневые, шурупы LN 3,5×9
6 — низ короба нижнего уровня — ГКЛ 12,5; шурупы TN 3,5×25 через 170 мм
7 — портьера
8 — стена с окном

Условные обозначения


— · — LED-лента в нише подсветки (карниз короба, ниша фигуры)

Примечания

1. Сечения потолков М 1:10 по помещениям с нишами LED и нишами под шторы: отметки и размеры этого помещения от ±0,000 чистого пола (м, мм). Положение — по плану потолков (лист 28): короб и ниша LED — по линиям ленты, ниша под шторы — у стены с окном; типовые узлы по группам помещений — на листе 29.
2. Крепёж: подвес прямой к плите на анкер-клине — по одному на подвес (Knauf П113); ПН к стенам — дюбель-гвоздь через ≤ 500 мм, не менее 3 на профиль (серия 1.045.9-2.08); лист 12,5 — шурупы TN 3,5×25 через 170 мм (СП 163, табл. 15); профили между собой — соединители одноуровневые, шурупы LN 3,5×9.
3. Изделие карниза, профиля LED и галтели подписано артикулом из данных; где артикул не выбран, сечение дано по габаритам из данных (ширина и глубина ниши, щель под свет), изделие подбирается по ним.

					Проект: Квартира 65 м²	М 1:10
	Лист	№ док.	Подпись	Дата		
Дизайнер	Кырлан А.С.			04.11.26	Сечения потолков М 1:10	Стадия / Лист / Листов
						П / 31 / 83

Условные обозначения

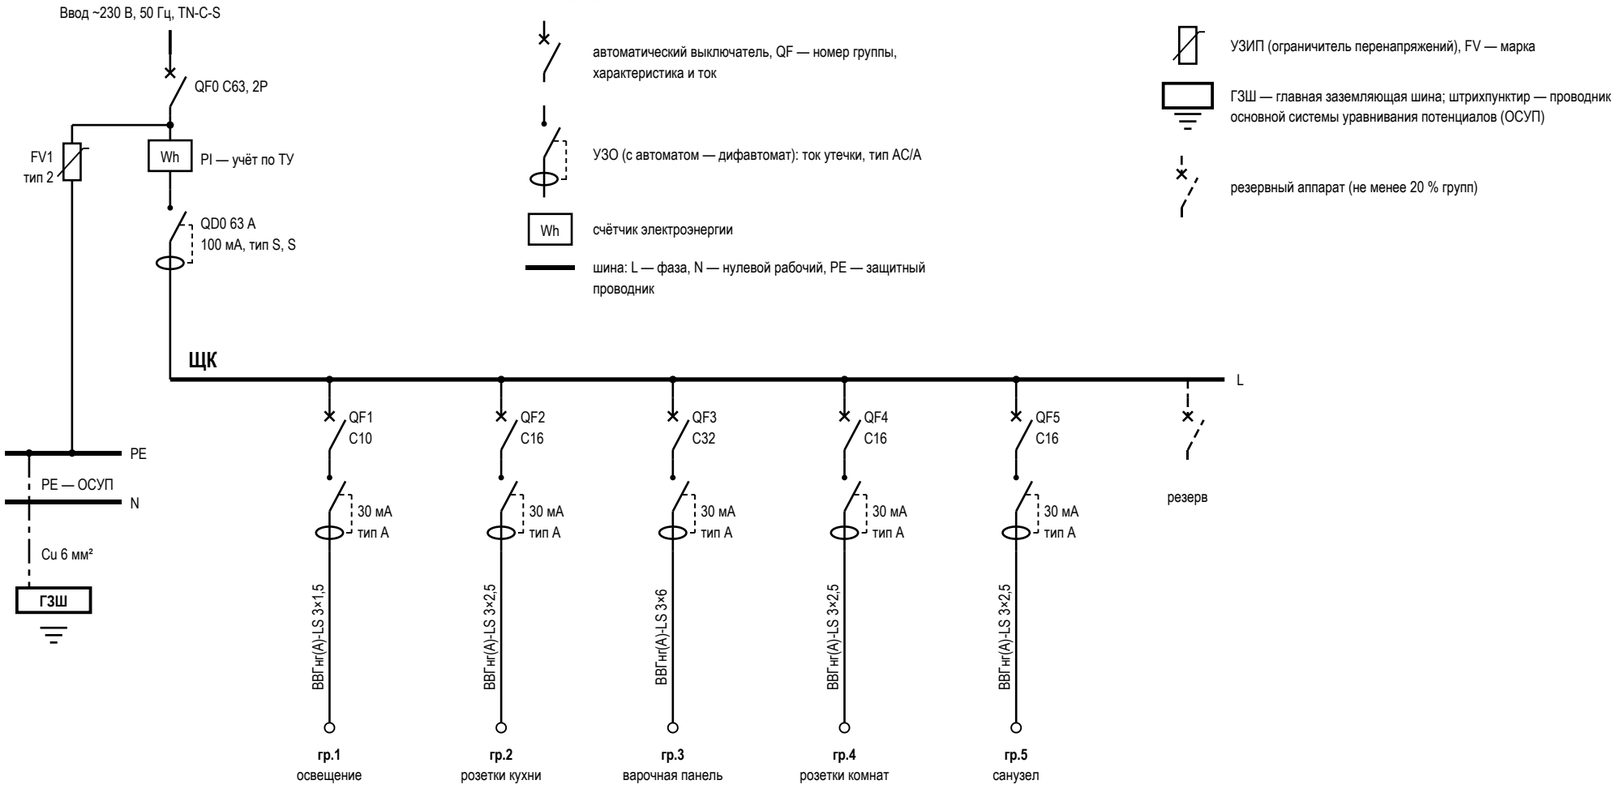

автоматический выключатель, QF — номер группы, характеристика и ток

УЗО (с автоматом — дифавтомат): ток утечки, тип AC/A

Wh — счётчик электроэнергии

шина: L — фаза, N — нулевой рабочий, PE — защитный проводник

УЗИП (ограничитель перенапряжений), FV — марка

ГЗШ — главная заземляющая шина; штрихпунктир — проводник основной системы уравнивания потенциалов (ОСУП)

резервный аппарат (не менее 20 % групп)

Данные щитка

Показатель	Значение
Номер щитка	ЩК
Тип	ЩРВ-П-24, IP41
Уст. мощность, кВт	
Разреш. мощность, кВт	15
Расчётная, кВт	9,8
Автоматы 1п: занят. / рез.	5 / 1
Модулей: всего / занято	24 / 16
Ток на вводе, А	63
Вводной аппарат	QF0 C63, 2P
УЗИП	FV1, тип 2, ЩК, после счётчика
ГЗШ, проводник ОСУП	Cu 6 мм²

Таблица групп щита ЩК и кабельный журнал

№	Назначение	Помещения	Автомат	УЗО / дифавтомат	Кабель	Длина, м	Р, кВт	Точек
1	освещение	1, 2, 3, 4, 5, 6, 7, 8, 9	C10	30 мА, тип A	ВВГнг(A)-LS 3×1,5	138,3		38
2	розетки кухни	3	C16	30 мА, тип A	ВВГнг(A)-LS 3×2,5	20,4		3
3	варочная панель	3	C32	30 мА, тип A	ВВГнг(A)-LS 3×6	17,2		1
4	розетки комнат	2, 3, 5	C16	30 мА, тип A	ВВГнг(A)-LS 3×2,5	52,4		10
5	санузел	7, 9	C16	30 мА, тип A	ВВГнг(A)-LS 3×2,5	47,1		9
	Итого по сечениям ВВГнг(A)-LS, м: 3×1,5 — 138,3; 3×2,5 — 119,9; 3×6 — 17,2					275,4		

Примечания

1. Схема однолинейная: одна линия — фаза, N и PE группы; аппараты — в отключённом положении (ГОСТ 2.702, ГОСТ 2.755). Номера групп — как у точек на планах (гр.). За отметку 0,000 принят уровень чистого пола; высота щита — по плану розеток.
2. Розеточные и мокрые линии — через УЗО или дифавтомат с током утечки не более 30 мА (ПУЭ 7.1.79); в санузле выполнить ДСУП (ПУЭ 7.1.87–7.1.88).
3. УЗО тип A — для линий с электроникой, стиральной и посудомоечной машиной, LED-драйверами; тип AC — только для чисто активной нагрузки.
4. Кабель — медный, исполнение нг(A)-LS (ГОСТ 31565-2012); скрытая прокладка только горизонтально и вертикально, фактические трассы зафиксировать исполнительной схемой до закрытия отделкой.
5. Номинал автомата — не выше допустимого тока кабеля: 1,5 мм² — до 10 А, 2,5 мм² — до 16 А. Резерв щита — не менее 20 % модулей.
6. Расчёт нагрузок, токов КЗ, селективности и сечений — по проекту ЭОМ организации с допуском СРО; лист задаёт состав, расположение и группы.
7. УЗИП FV1 — после вводного автомата, проводник к шине PE — кратчайший, без петель. Шина PE щита соединяется с ГЗШ проводником ОСУП; к ГЗШ присоединяются трубы водопровода и отопления на вводе в квартиру (ПУЭ 7.1.87). Шины N и PE — раздельные, после разделения PEN не объединяются.
8. До подключения нагрузки — приёмо-сдаточные испытания с протоколом: сопротивление изоляции линий не менее 0,5 МОм, срабатывание УЗО по току и времени, непрерывность защитных проводников PE (ПУЭ, гл. 1.8).

					Проект: Квартира 65 м²
	Лист	№ док.	Подпись	Дата	Однолинейная схема щита
Дизайнер	Кырлан А.С.			04.11.26	

Стадия	Лист	Листов
П	32	83

Условные обозначения

Знак	Тип изделия	H, мм	Кол., шт
	Розетка с заземлением	300	10
	То же	у знака	6
	Блок розеток с заземлением, рамка 2 поста	у знака	3
	Розетка с заземлением IP44	1100	2
	Вывод кабеля к прибору	у знака	4
	КУП (уравнивание потенциалов)	300	1
ЩК	Щит квартирный	1700	1

розетка с заземляющим контактом; у знака — марка, ×N — постов в рамке, гр. — группа щита, H — высота оси, мм

знак разведён для читаемости: точка на стене — у выноски, привязка — до неё


граница зоны 2 ванной (600 мм от ванны/поддона)

мебель и сантехприборы — подложка

стояк: К1 — канализация, В1 — ХВС, Т3 — ГВС

1 номер помещения, площадь м²


Итого розеток (механизмов) — 24 шт; рамок — 21 шт: на 1 пост — 18, на 2 поста — 3.

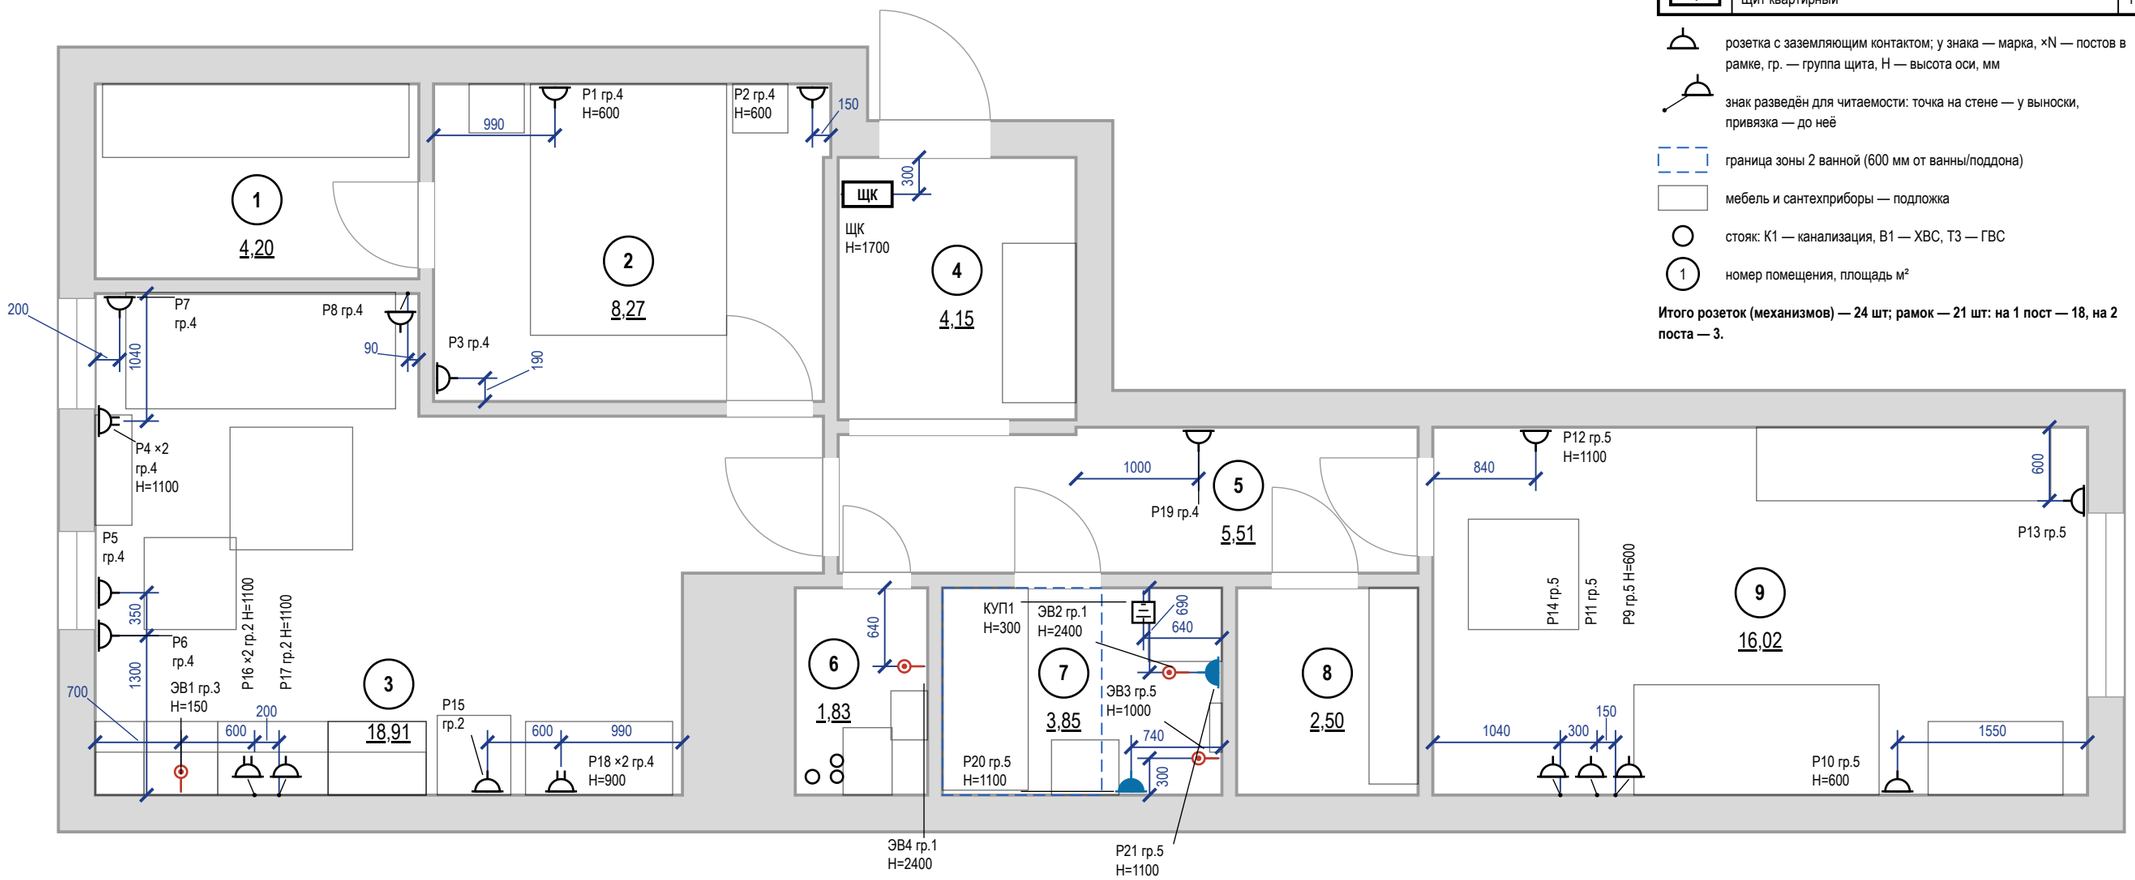

Примечания

1. За отметку 0,000 принят уровень чистого пола. Высоты H — от чистого пола до оси изделия; привязки — от чистовой грани стены до оси механизма (у рамки на несколько постов — до оси рамки).
2. Розетки без отметки H у знака — на высоте 300 мм от чистого пола до оси механизма; выводы кабеля — по паспорту прибора.
3. Розетки в санузле — только вне зон 0–2 (ПУЭ 7.1.48, ГОСТ Р 50571.7.701-2024), IP44, через УЗО 30 мА.
4. Розеточные и мокрые линии — через УЗО или дифавтомат с током утечки не более 30 мА (ПУЭ 7.1.79); в санузле выполнить ДСУП (ПУЭ 7.1.87–7.1.88).
5. Кабель — медный, исполнение нг(А)-LS (ГОСТ 31565-2012); скрытая прокладка только горизонтально и вертикально, фактические трассы зафиксировать исполнительной схемой до закрытия отделкой.
6. Расчёт нагрузок, токов КЗ, селективности и сечений — по проекту ЭОМ организации с допуском СРО; лист задаёт состав, расположение и группы.
7. Выводы кухонной техники — после утверждения проекта кухни (ориентировочно); привязки выводов даны от осей модулей гарнитура и пересматриваются вместе с проектом кухни.

					Проект: Квартира 65 м² — **М 1:50**
	Лист	№ док.	Подпись	Дата	План розеток и электровыводов
Дизайнер	Кырлан А.С.			04.11.26	Стадия: П; Лист: 33; Листов: 83

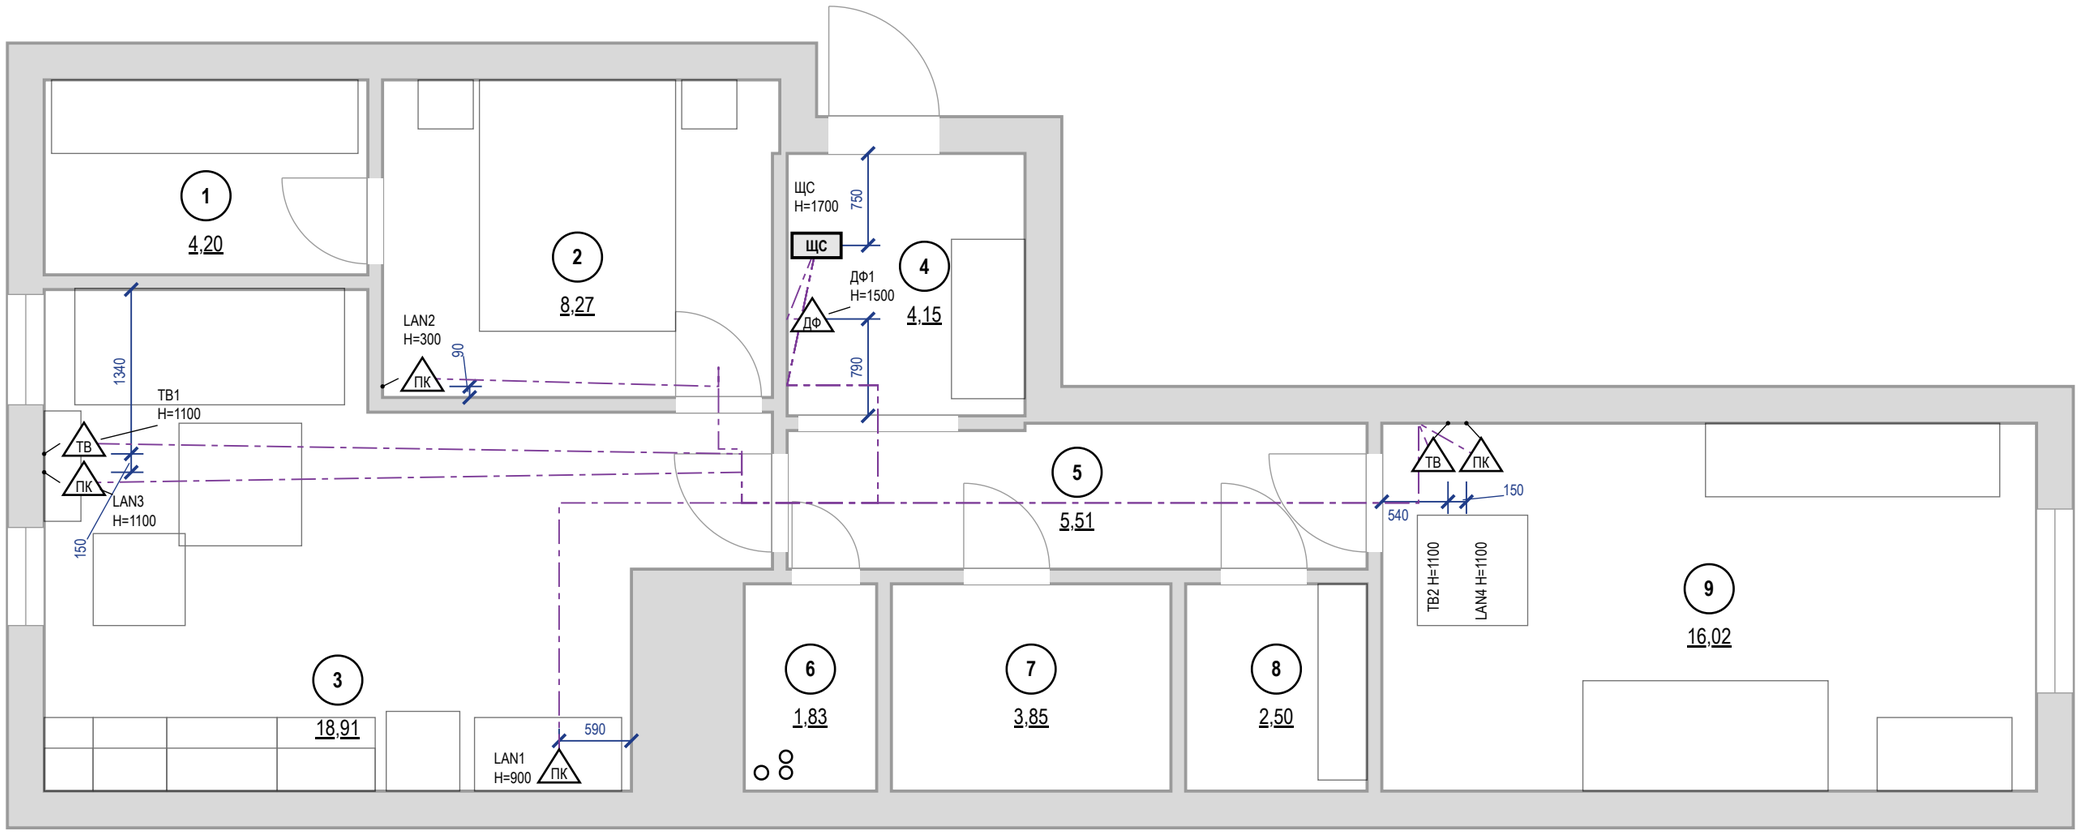

Примечания


1. За отметку 0,000 принят уровень чистого пола. Высоты Н — от чистого пола до оси изделия; привязки — от чистовой грани стены до оси механизма (у рамки на несколько постов — до оси рамки).
2. Высота установки, не указанная на плане: розетки LAN и ТВ — 300 мм от чистого пола.
3. Слаботочные кабели — отдельно от силовых: в своей трубе или лотке, при параллельной прокладке не ближе 100 мм к силовым, пересечения под прямым углом; каждую точку — отдельным кабелем от ЩС без скруток.
4. Трассы на листе — принципиальные; фактические зафиксировать исполнительной схемой до закрытия отделкой. Силовые линии, УЗО 30 мА, ДСУП, кабель нг(А)-LS — по листам розеток и щита.
5. Проект силовой части и расчёт токов КЗ — по проекту ЭОМ; слаботочная часть согласуется с провайдером и управляющей компанией (домофон, коллективное ТВ).

Условные обозначения

- ЩС — щит слаботочный: ввод провайдера, роутер, коммутатор
- ПК — розетка компьютерная RJ45
- ТВ — розетка телевизионная
- ДФ — трубка или монитор домофона
- кабель от ЩС до точки, отдельным лучом
- мебель и сантехприборы — подложка
- стояк: К1 — канализация, В1 — ХВС, Т3 — ГВС
- 1 — номер помещения, площадь м²

					Проект: Квартира 65 м²	М 1:50
	Лист	№ док.	Подпись	Дата	План слаботочных сетей	Стадия / Лист / Листов
Дизайнер	Кырлан А.С.			04.11.26		П / 34 / 83

выпуск 04.11.2026 № 84932ed378 · стр. 34 из 83

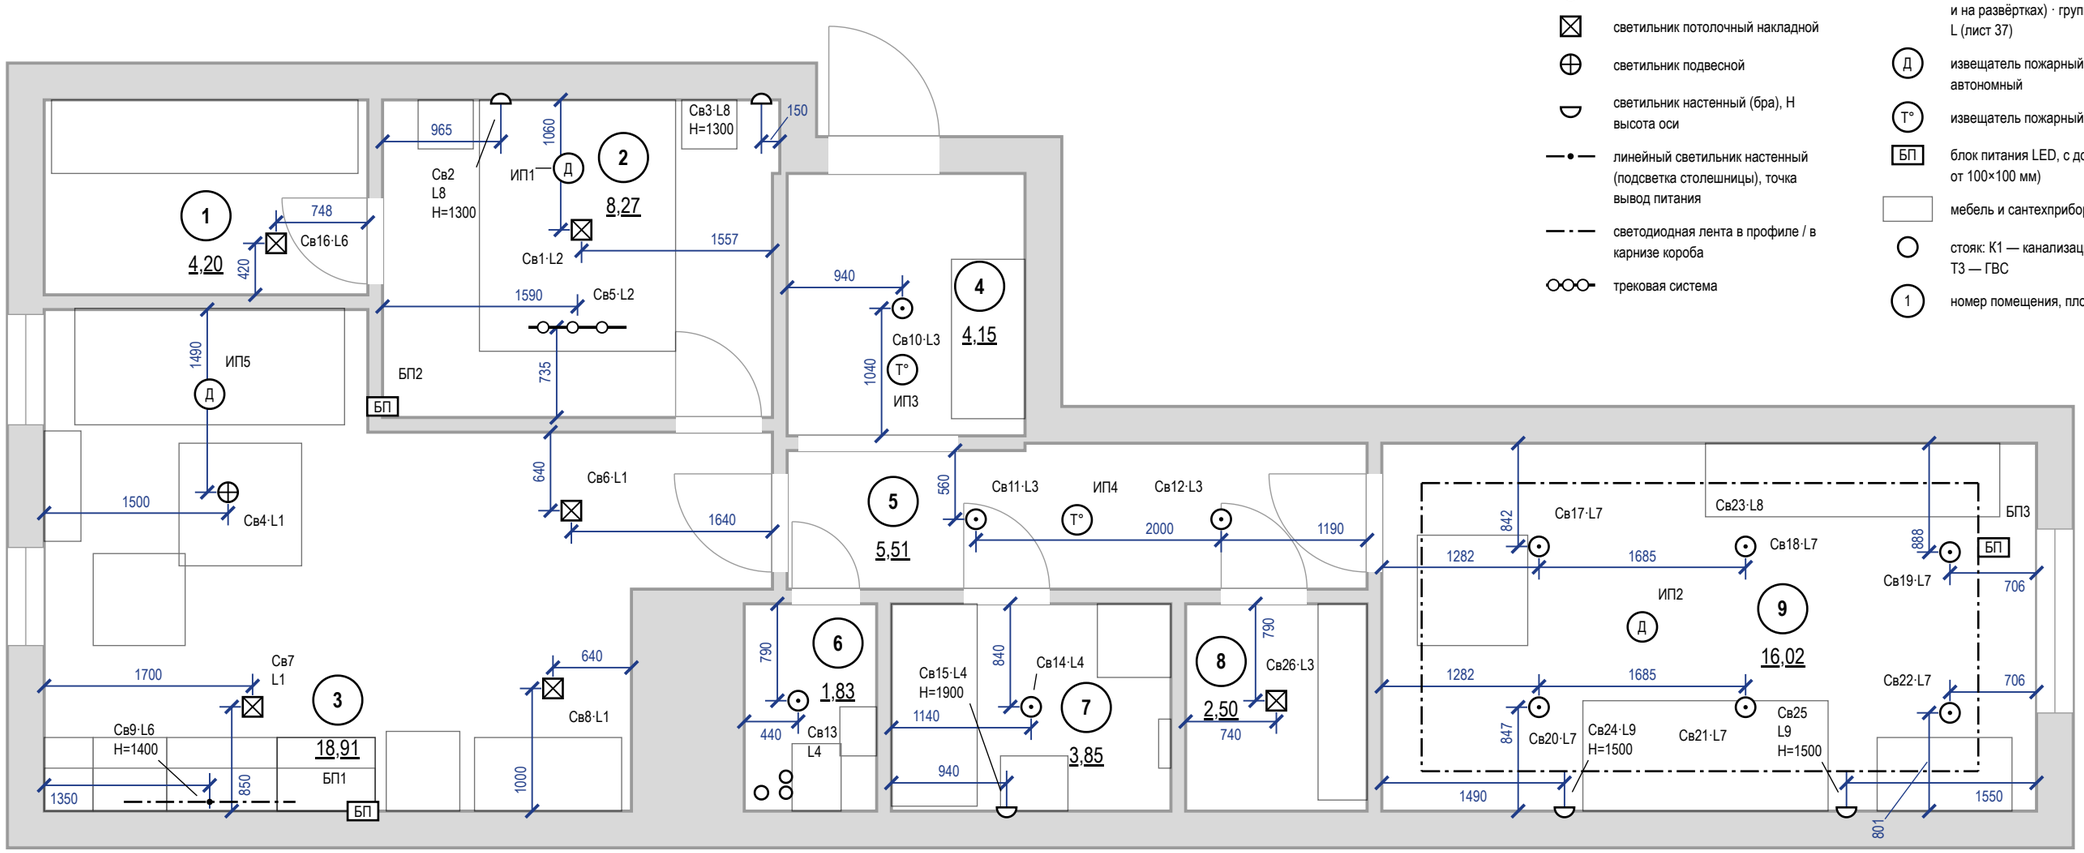

Условные обозначения

- светильник встраиваемый точечный
- светильник потолочный накладной
- светильник подвесной
- светильник настенный (бра), H высота оси
- линейный светильник настенный (подсветка столешницы), точка вывод питания
- светодиодная лента в профиле / в карнизе короба
- трековая система
- Св1·L1 — марка светильника (как в ведомости и на развёртках) · группа включения L (лист 37)
- Д — извещатель пожарный дымовой автономный
- Т° — извещатель пожарный тепловой
- БП — блок питания LED, с доступом (люк от 100×100 мм)
- мебель и сантехприборы — подложка
- стояк: К1 — канализация, В1 — ХВС, Т3 — ГВС
- 1 — номер помещения, площадь м²

Примечания

1. За отметку 0,000 принят уровень чистого пола. Высоты H — от чистого пола до оси изделия; привязки — от чистовой грани стены до оси механизма (у рамки на несколько постов — до оси рамки).
2. Высота установки, не указанная на плане: светильники — на потолке; настенные — по отметке H у знака. Привязки — до оси светильника от чистовой грани стены, по рядам.
3. Во влажных помещениях — светильники не ниже IP44; в зонах 0–2 ванной — по ГОСТ Р 50571.7.701-2024 (зона 1 — IPX5).
4. LED-лента в карнизе подсветки короба — по линии карниза с плана потолков; блок питания — в люке короба (БП на плане), питание ленты длиннее 5 м — с двух концов.
5. Розеточные и мокрые линии — через УЗО или дифавтомат с током утечки не более 30 мА (ПУЭ 7.1.79); в санузле выполнить ДСУП (ПУЭ 7.1.87–7.1.88).
6. Кабель — медный, исполнение нг(A)-LS (ГОСТ 31565-2012); скрытая прокладка только горизонтально и вертикально, фактические трассы зафиксировать исполнительной схемой до закрытия отделкой.
7. Расчёт нагрузок, токов КЗ, селективности и сечений — по проекту ЭОМ организации с допуском СРО; лист задаёт состав, расположение и группы.
8. Ведомость светильников (тип, количество, мощность, поток, Tц, Ra) — лист 36.

	Лист	№ док.	Подпись	Дата
Дизайнер	Кырлан А.С.			04.11.26

Проект: Квартира 65 м² — **М 1:50**

План освещения

Стадия	Лист	Листов
П	35	83

Параметры светильников для подбора

Поз.	Марки	Наименование	Установка	Кол.	P, Вт	Σ P, Вт	Ф, лм	Тц, К	Ra	Угол, °	IP	Дим.	Слой	Группа	Пом.
1	Св16	Потолочный накладной	на потолке, засветка стены	1	10	10	900	3000	90	—	20	—	общий	L6	1
2	Св1	Потолочный накладной	на потолке	1	36	36	3200	2700	90	—	20	—	общий	L2	2
3	Св5	Трековая система	на потолке	2	12	24	900	2700	90	—	20	—	общий	L2	2
4	Св2, Св3	Настенный (бра)	на стене, H=1300	2	4	8	250	2700	90	—	20	—	рабочий	L8	2
5	Св4	Подвесной	подвес	1	24	24	2400	3000	90	—	20	—	общий	L1	3
6	Св6	Потолочный накладной	на потолке	1	18	18	1800	3000	90	—	20	—	общий	L1	3
7	Св7	Потолочный накладной	на потолке	1	12	12	1100	3000	90	—	20	—	общий	L1	3
8	Св8	Потолочный накладной	на потолке	1	12	12	1000	4000	90	—	20	—	общий	L1	3
9	Св9	Линейный настенный	под верхними шкафами, H=1400	1	18	18	1300	3000	90	—	20	—	рабочий	L6	3
10	Св10–Св12	Встраиваемый точечный	в ГКЛ, корпус ≤ 70 мм	3	9	27	800	3000	90	—	20	—	общий	L3	4, 5
11	Св13	Встраиваемый точечный	в ГКЛ, корпус ≤ 70 мм	1	6	6	500	3000	90	—	20	—	общий	L4	6
12	Св14	Встраиваемый точечный	в ГКЛ, корпус ≤ 70 мм	1	9	9	700	3000	90	—	44	—	общий	L4	7
13	Св15	Настенный (бра)	над зеркалом, H=1900	1	6	6	400	3000	90	—	44	—	рабочий	L4	7
14	Св26	Потолочный накладной	на потолке	1	9	9	600	3000	90	—	20	—	общий	L3	8
15	Св17–Св22	Встраиваемый точечный	в ГКЛ, корпус ≤ 70 мм	6	12	72	1050	2700	90	—	20	—	общий	L7	9
16	Св23	Лента светодиодная 24 В	в карнизе короба, профиль с рассеивателем	13,8 м	9,6/м	132,3	900/м	2700	90	—	20	да	акцентный	L8	9
17	Св24, Св25	Настенный (бра)	на стене, H=1500	2	6	12	400	2700	90	60	20	—	рабочий	L9	9
		Итого		**26 шт + 13,8 м**		**435,3**									

LED-ленты, линейные светильники и блоки питания


Марка	Пом.	L, м	U, В	Вт/м	Σ P, Вт	БП	P БП, Вт	Загр., %	Питание	Доступ к БП
Св5	2	0,8	24	—	24	БП2	60	40	встроенный ввод	H=2300
—	3	2,5	24	—	18	БП1	60	30	встроенный ввод	H=2300
Св23	9	13,8	24	9,6	132,3	БП3	200	66	с двух концов	люк 300×300 в коробе потолка ПТ3

Примечания

1. Позиции и марки Св — те же, что на плане освещения (лист 35); группы L — по плану выключателей (лист 37).
2. Модели светильников не выбраны: лист — техническое задание на подбор. Модель по строке таблицы: поток, Тц, Ra, угол, IP и регулировка яркости не хуже указанных, мощность не больше; встраиваемые — под глубину короба (графа «Установка»). IP 20 — сухие помещения. После выбора моделей (артикул, производитель) лист выпускается как «Спецификация светильников».
3. Длина LED-ленты в карнизе — по линии карниза плана потолков (лист 28); Σ P = Вт/м × длина. Блок питания загружен не больше чем на 80 %; лента 24 В длиннее 10 м питается с двух концов; доступ к блоку питания — люк ревизии 300×300 мм или место, указанное в таблице.
4. В пом. 9 свет включается клавишами групп — лист 37.
5. Мощность и поток в таблице — требования к подбору (поток не меньше, мощность не больше указанных); после выбора модели — по её паспорту, Σ P — установленная мощность освещения. Оценка освещённости — на плане освещения; это не светотехнический расчёт.

					Проект: Квартира 65 м²
	Лист	№ док.	Подпись	Дата	Техническое задание на подбор светильников
Дизайнер	Кырлан А.С.			04.11.26	

Стадия	Лист	Листов
П	36	83

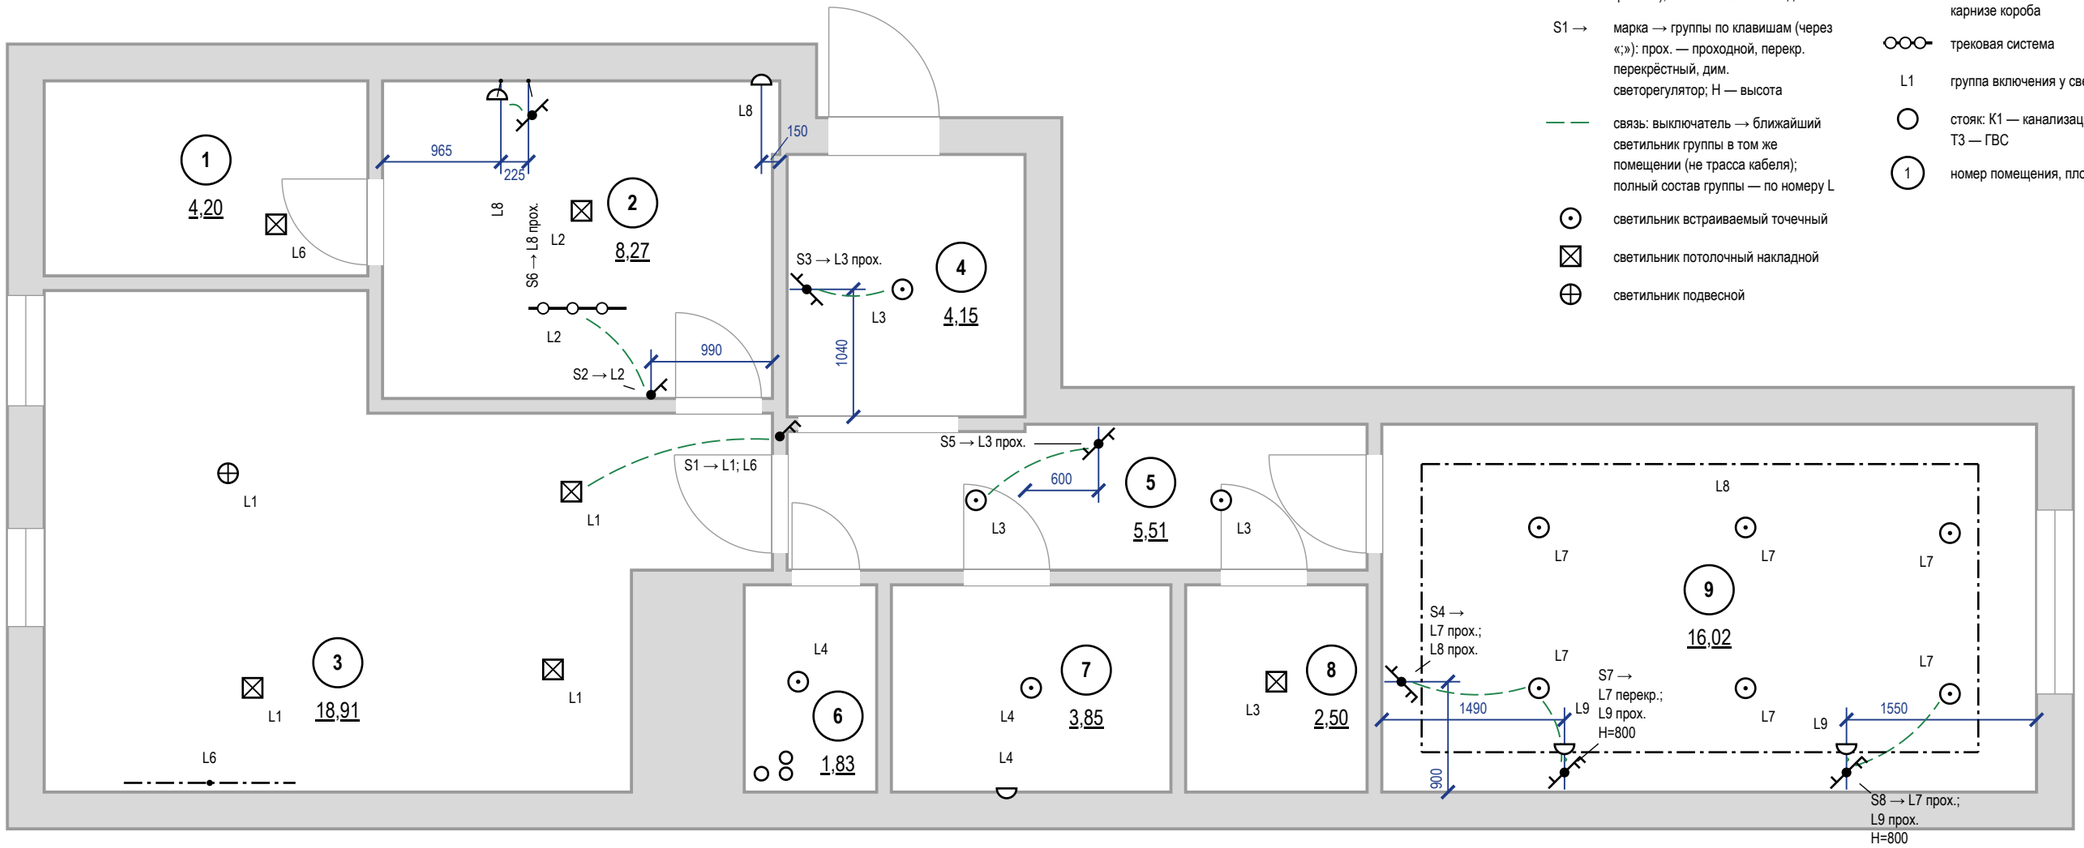

Условные обозначения

- выключатель одноклавишный
- выключатель двухклавишный (флажков — по числу клавиш)
- выключатель с проходной или перекрёстной клавишей (обратный флажок); тип клавиши — в подписи
- S1 → марка → группы по клавишам (через «;»): прох. — проходной, перекр. перекрёстный, дим. светорегулятор; H — высота
- связь: выключатель → ближайший светильник группы в том же помещении (не трасса кабеля); полный состав группы — по номеру L
- светильник встраиваемый точечный
- светильник потолочный накладной
- светильник подвесной
- светильник настенный (бра), H высота оси
- линейный светильник настенный (подсветка столешницы), точка вывод питания
- светодиодная лента в профиле / в карнизе короба
- трековая система
- L1 группа включения у светильника
- стояк: К1 — канализация, В1 — ХВС, Т3 — ГВС
- 1 номер помещения, площадь м²


Примечания

1. За отметку 0,000 принят уровень чистого пола. Высоты H — от чистого пола до оси изделия; привязки — от чистовой грани стены до оси механизма (у рамки на несколько постов — до оси рамки).
2. Высота установки, не указанная на плане: выключатели — 900 мм от чистого пола (у кровати и другие — H у марки), со стороны дверной ручки (ПУЭ 7.1.51).
3. Какой выключатель какие светильники включает — по номеру группы L: у выключателя (S1 → L1; L2 — клавиши по порядку) и у каждого светильника. Пунктир подсказка к ближайшему светильнику группы в том же помещении (не дальше 3 м), это не трасса кабеля; выключатель за стеной (у двери санузла) и далёкая группа — только номер группы.
4. Группы из нескольких мест (L8 — S4, S6; L3 — S3, S5; L7 — S4, S7, S8; L9 — S7, S8): на крайних местах — проходные клавиши, на промежуточных — перекрёстные; механизмы — в ведомости изделий.
5. Вентиляторы санузлов (выводы ЭВ на плане розеток) включаются вместе с основным светом помещения, отключаются с задержкой — таймер выбега в вентиляторе.
6. Розеточные и мокрые линии — через УЗО или дифавтомат с током утечки не более 30 мА (ПУЭ 7.1.79); в санузле выполнить ДСУП (ПУЭ 7.1.87–7.1.88).
7. Кабель — медный, исполнение нг(A)-LS (ГОСТ 31565-2012); скрытая прокладка только горизонтально и вертикально, фактические трассы зафиксировать исполнительной схемой до закрытия отделкой.
8. Расчёт нагрузок, токов КЗ, селективности и сечений — по проекту ЭОМ организации с допуском СРО; лист задаёт состав, расположение и группы.
9. Группы без выключателя: L4 — назначить управление до монтажа.

					Проект: Квартира 65 м²	М 1:50
	Лист	№ док.	Подпись	Дата	Управление светильниками	Стадия / Лист / Листов
Дизайнер	Кырлан А.С.			04.11.26		П / 37 / 83

Условные обозначения

- стояк: К1 — канализация, В1 — ХВС, Т3 — ГВС
- номер помещения, площадь м²
- вытяжная решётка в вентканал: марка, расход м³/ч, Н центра от чистого пола
- вытяжная решётка с бытовым вентилятором и обратным клапаном: марка, расход, Н
- приточный клапан (КИВ) в наружной стене: марка, расход, Н центра
- бризер (приток с фильтром и подогревом)
- переток: зазор под полотном или переточная решётка
- кухонная вытяжка над варочной панелью
- Вентканал ВК-N.
- воздуховод в коробе под потолком (за подшивным потолком) до вентканала
- отдельный вход воздуховода в вентканал, обратный клапан

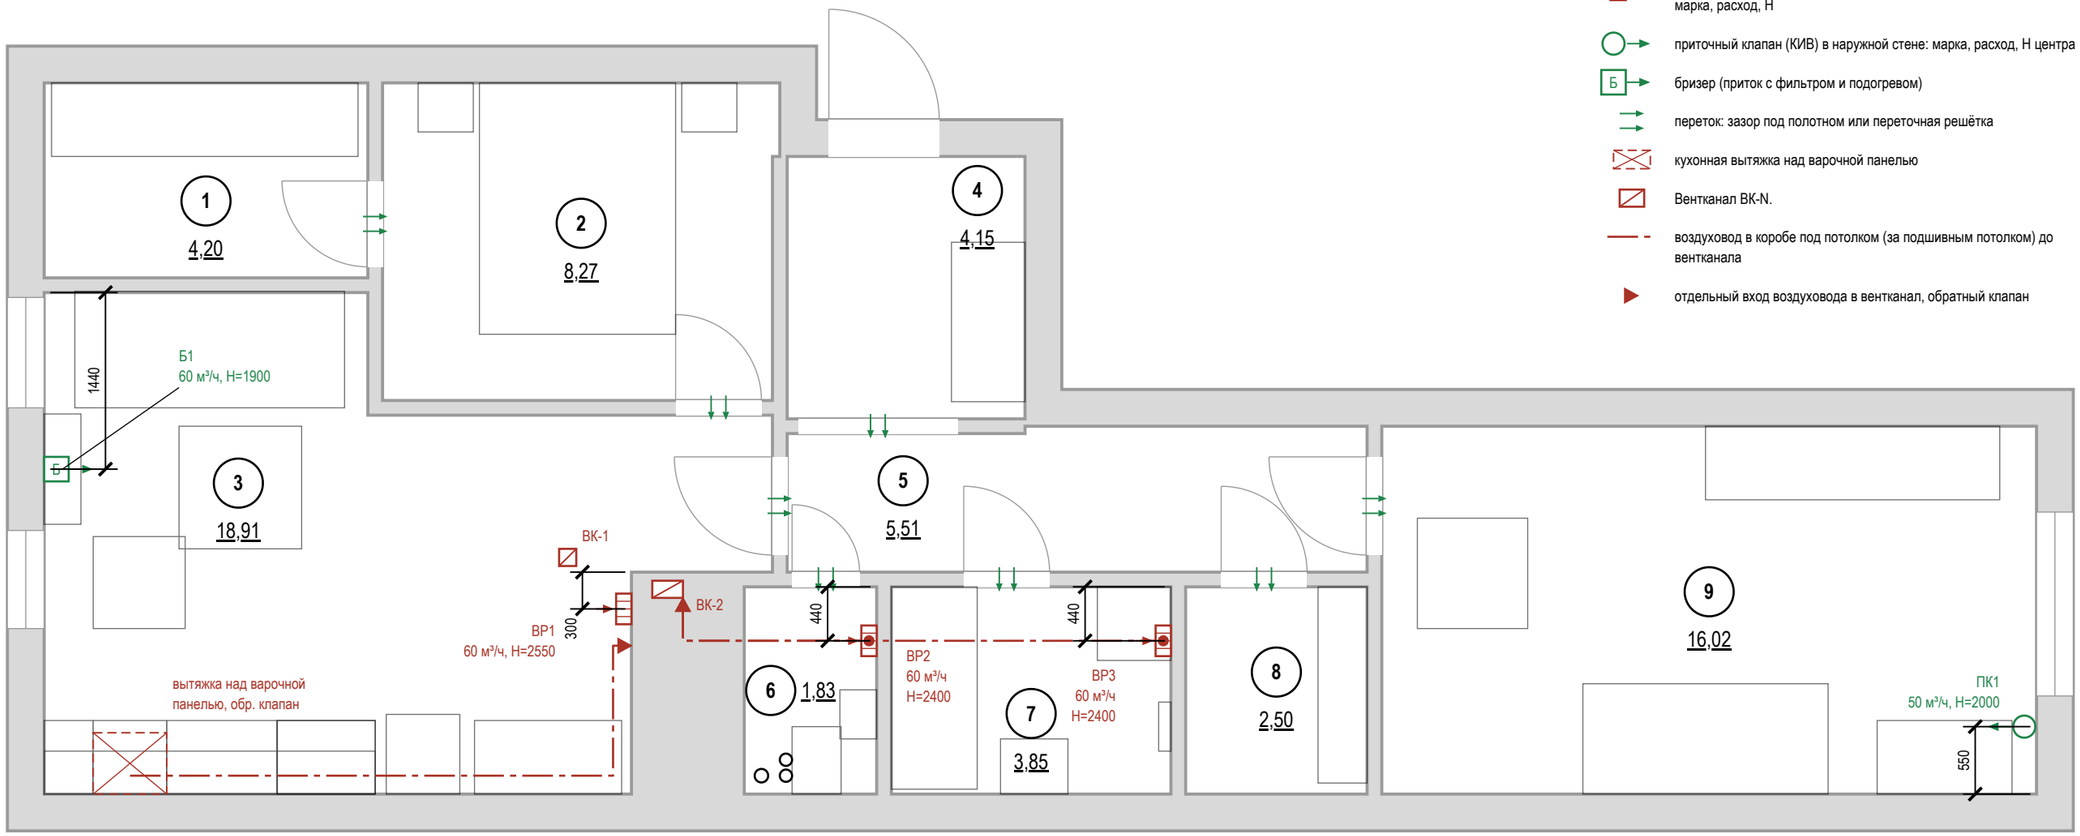


Примечания

1. Расчёт систем ОВ и подбор оборудования — проектная организация с допуском СРО; лист даёт места, трассы и привязки.
2. Нормы вытяжки — СП 54.13330.2022 (Изм. 1, 2), табл. 7.1: кухня с электроплитой 60 м³/ч, с газовой 100; ванная и совмещённый санузел 50; уборная 25; гардеробная 0,2 ч⁻¹. Приток в жилые — 3 м³/ч на 1 м² (менее 20 м² общей площади на человека), иначе 30 м³/ч на человека.
3. Вентканалы и шахты не сужать, не переносить и не закрывать; вентилятор и кухонная вытяжка — через обратный клапан, без перекрытия естественной тяги; ВР2 — воздуховодом до ВК-2 ≈ 1,9 м, ВР3 — воздуховодом до ВК-2 ≈ 4,3 м в коробе под потолком.
4. Проектные расходы — не ниже нормы, вытяжка сведена с притоком вентиляторами мокрых помещений. Клапаны — в простенке у окна, центр 2000 мм, не над кроватью, не ближе 300 мм к стоякам отопления; типоразмер — на расход.
5. Кухонная вытяжка в воздухообмен не включена: воздуховод не менее Ø125 в коробе, вход в канал отдельный.
6. Переток — зазор под полотнами межкомнатных дверей или переточная решётка.
7. Кондиционирование заданием не предусмотрено; при установке трассы фреона и дренажа (не менее 40 мм/м, в К1 через сифон) и питание заложить до черновых работ.
8. Привязки оборудования — по паспортам приобретённых моделей, до черновых работ.
9. Привязки — до обмера: вентканалы ВК-N приняты проектировщиком, решётки и воздуховоды — от них. До черновых работ — обмер каналов и тяги, лист перевыпустить по факту.

					Проект: Квартира 65 м² — **М 1:50**
	Лист	№ док.	Подпись	Дата	План вентиляции — Стадия: П; Лист: 38; Листов: 83
Дизайнер	Кырлан А.С.			04.11.26	

выпуск 04.11.2026 № 84932ed378 · стр. 38 из 83

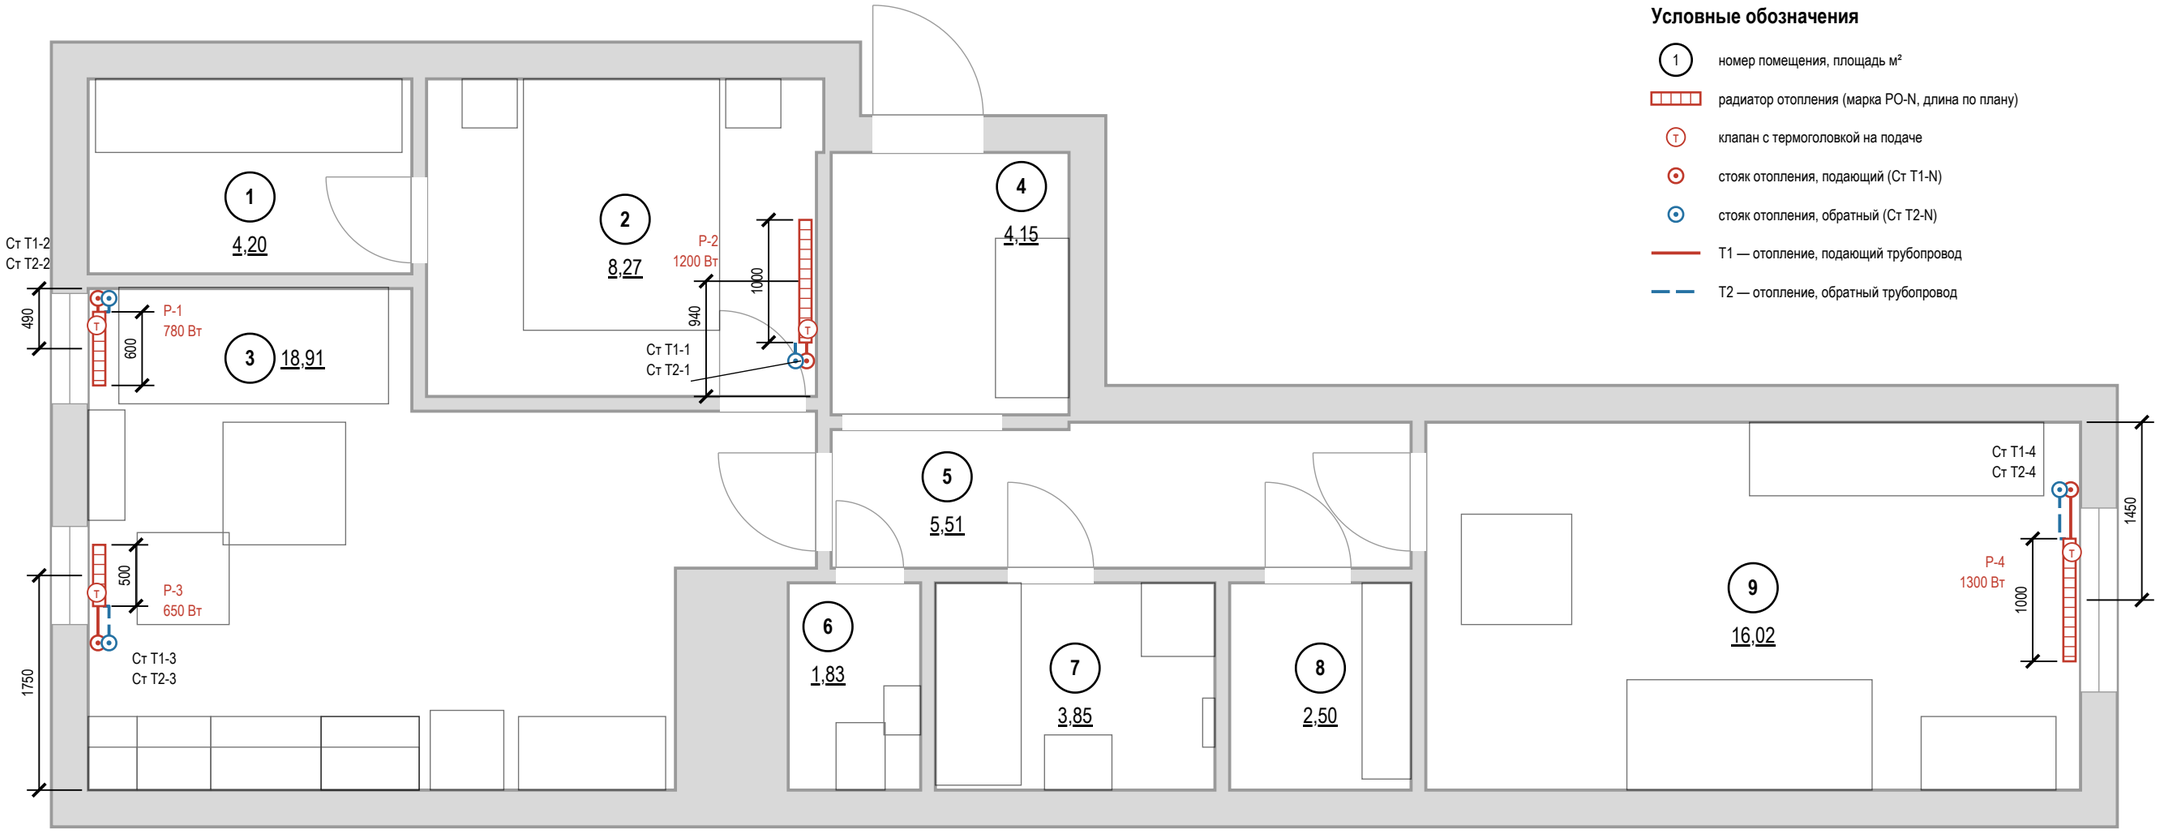

Условные обозначения

- 1 — номер помещения, площадь м²
- радиатор отопления (марка РО-N, длина по плану)
- клапан с термоголовкой на подаче
- стояк отопления, подающий (Ст Т1-N)
- стояк отопления, обратный (Ст Т2-N)
- Т1 — отопление, подающий трубопровод
- Т2 — отопление, обратный трубопровод

Примечания

1. Расчёт системы отопления, теплопотерь и подбор приборов — проектная организация с допуском СРО; лист даёт места и привязки.
2. Тип, длина и мощность радиаторов — по теплотехническому расчёту; лист задаёт места, зазоры и подключение.
3. Зазоры радиатора: низ не менее 100 мм от чистого пола, верх не менее 100 мм до подоконника, 30–50 мм от стены до задней панели; центр по оси окна с допуском ±20 мм. Верх до подоконника — 180 мм.
4. Радиаторы не закрывать глухими коробами и мебелью; перенос и замена приборов в многоквартирном доме — переустройство, согласование с управляющей организацией (ЖК РФ ст. 25–26); вынос на лоджию запрещён.
5. Трубы отопления через межквартирные стены не прокладывать (СП 51.13330.2011, п. 9.19); через перекрытия и перегородки — в гильзах.
6. Привязки приборов и подводок — по паспортам приобретённых радиаторов и клапанов, до черновых работ.
7. Привязки — до обмера: Стояки отопления в исходных данных не заданы: показаны у откосов окон и у торцов приборов, подводки — принципиально. До черновых работ — обмер стояков и паспорта приборов; лист перевыпустить по факту.
8. До закрытия отделкой трубопроводы отопления испытать гидростатическим давлением с оформлением акта (СП 73.13330.2016, 7.2–7.3).

					Проект: Квартира 65 м² — М 1:50
	Лист	№ док.	Подпись	Дата	
Дизайнер	Кырлан А.С.			04.11.26	План отопления



Стадия	Лист	Листов
П	39	83

выпуск 04.11.2026 № 84932ed378 · стр. 39 из 83

Спецификация плинтусов


Наименование	Помещения	Длина, м (с запасом)
SX165, h = 69 мм, крепление к стене, окраска в цвет Tikkurila V503	1	9
SX165, h = 69 мм, крепление к стене, окраска в цвет NCS S 0300-N	2, 3, 4, 5, 8	53
SX165, h = 69 мм, крепление к стене, окраска в цвет Farrow & Ball No. 241	9	18

Экспликация полов

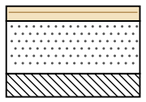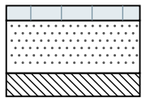Номер помещения	Тип пола	Схема пола	Данные элементов пола (наименование, толщина, основание), мм	Площадь, м²
1, 2, 3, 8, 9	1		Инженерная доска на клею — 14 Стяжка ЦПС М200 — 50 Плита перекрытия Всего 64 мм; ЧП ±0,000, верх плиты −0,064	49,90
4, 5	2		Керамогранит на клею С2 TE S1 — 14 Стяжка ЦПС М200 — 50 Плита перекрытия Всего 64 мм; ЧП ±0,000, верх плиты −0,064	9,66
6, 7	3		Керамогранит на клею С2 TE S1 — 14 Гидроизоляция обмазочная, 2 слоя, с заведением на стены 200 мм — 2 Стяжка ЦПС М200 — 33 Плита перекрытия Всего 49 мм; ЧП −0,015, верх плиты −0,064	5,68
			Итого	**65,24**

Отметки по высоте

±0,000 чистый пол пом. 1–5, 8, 9; отсчёт высот
−0,015 чистый пол пом. 6, 7, ниже на 15 мм
−0,064 верх плиты — расчёт, не замер (задание на обмер)
сущ. пол снимается до плиты; не замерен (задание на обмер)

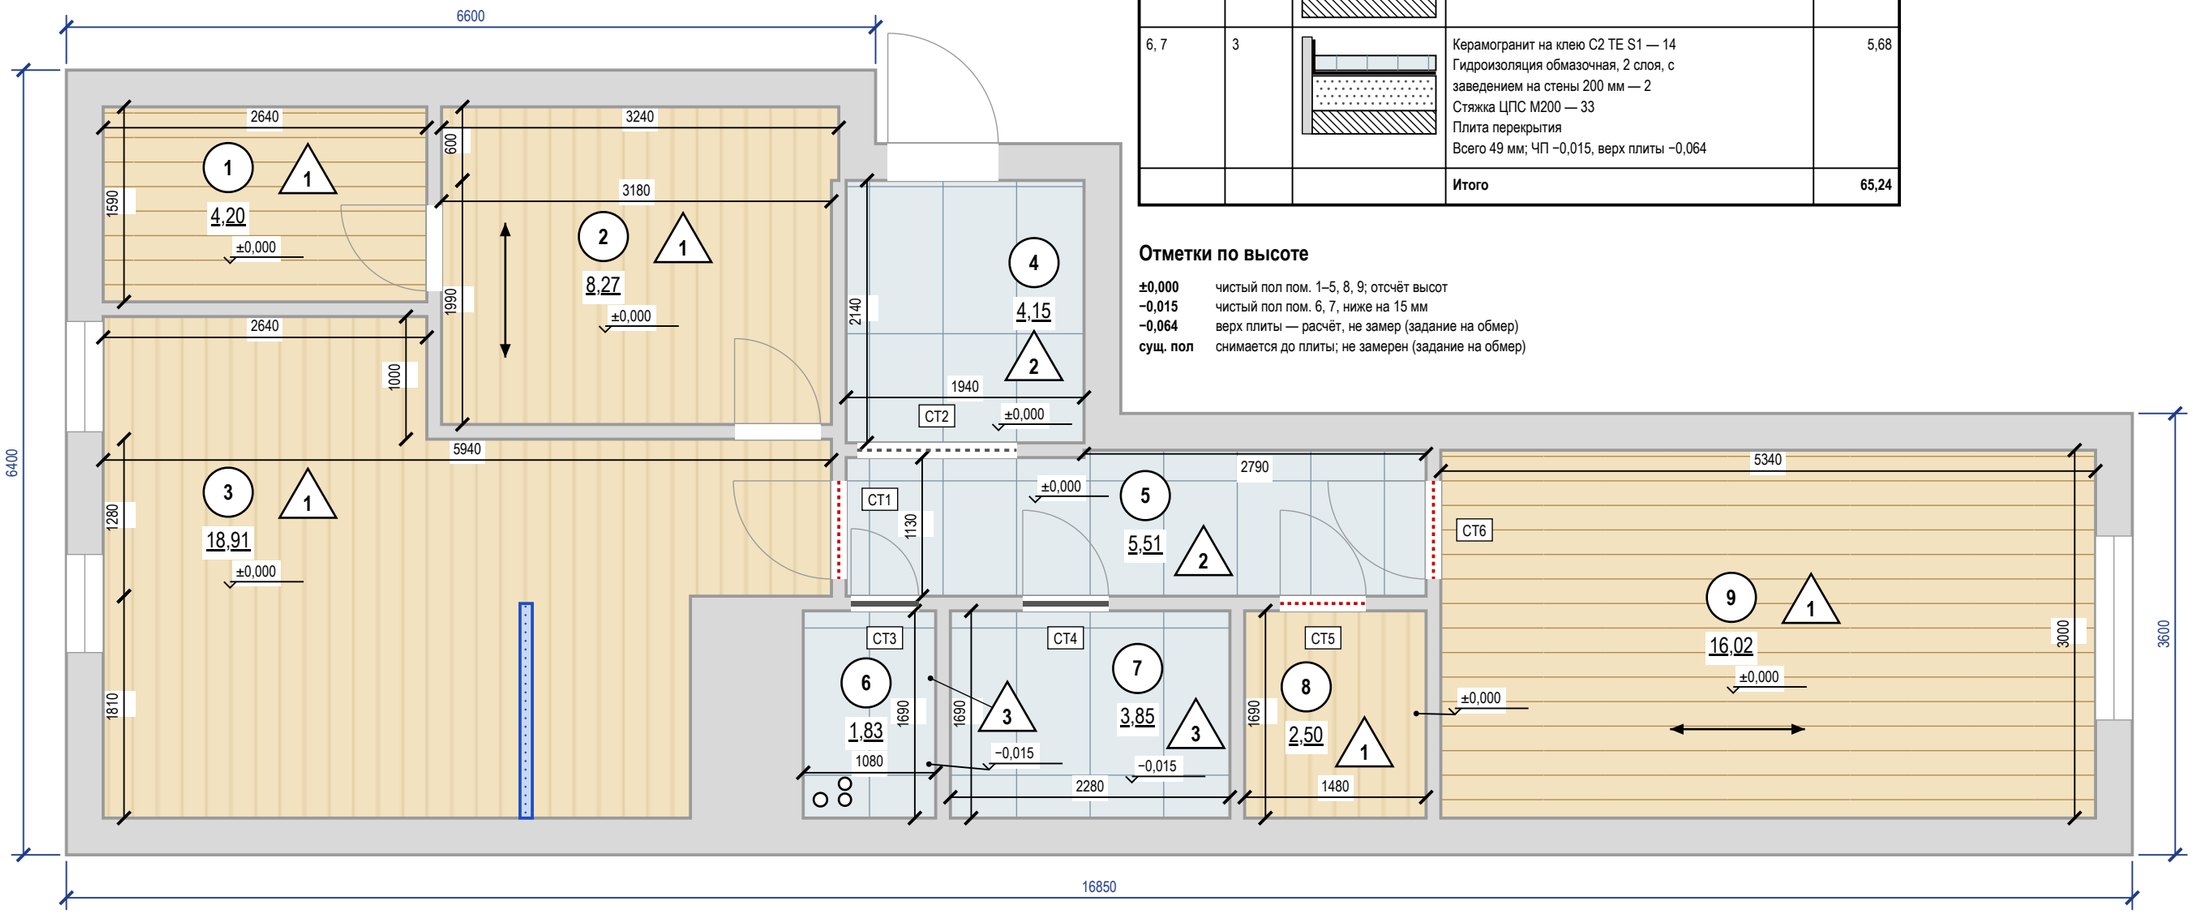


Примечания


1. За отметку ±0,000 принят чистый пол, не существующий (блок отметок). Площади — по чистым размерам помещений, м²; размеры — в мм.
2. Стык разнотипных покрытий — по оси дверного полотна (под полотном в закрытом положении); решение стыка — по ведомости стыков.
3. Размеры помещений в свету (ширина × длина, мм), не поместившиеся на плане: пом. 3 — 2640 × 1000, 5940 × 1280, 4790 × 1810; пом. 5 — 2790 × 60, 4730 × 1130.
4. Пол санузлов ниже смежных помещений на 15 мм за счёт меньшей толщины стяжки (верх плиты общий — по экспликации полов); гидроизоляция по стяжке с заведением на стены не менее 200 мм (СП 29.13330.2011, п. 7.2), до облицовки — тест проливом и акт скрытых работ.
5. Выпуски канализации с уклоном и трассы водоснабжения — в слое засыпки под стяжкой (по экспликации полов); отметки, уклоны и прочистки — по листу разводки ВК 16.
6. Звукоизоляционный слой под стяжкой проектом не предусмотрен (стяжка по плите): приведённый уровень ударного шума перекрытия с полом Lnw не более 60 дБ (СП 51.13330.2011, табл. 2) подтвердить по данным дома; при превышении — плавающая стяжка по звукоизоляции с демпферной лентой по контуру и у стояков, пирог пересчитать.
7. Штучные покрытия (инженерная доска): направление — по стрелке; влажность основания по СМ не более 2,0 % (по ТУ изготовителя).
8. Ровность основания — просвет под 2-метровой рейкой не более 2 мм: пом. 1, 2, 3, 8, 9 (инженерная доска), пом. 4, 5, 6, 7 (керамогранит); проверить до укладки покрытия (СП 71.13330.2017, табл. 8.5).
9. Сетка на плитке — условная, в размер формата; точка старта и раскладка — по листу раскладки плитки.
10. Узор покрытия (заливка-код типа пола) прерывается под надписями — площадями помещений и отметками чистого пола.
11. Пироги полов — по экспликации полов: слои сверху вниз, толщины в мм; гидроизоляция мокрых зон — в пироге и в ведомости отделки; схема пола — без масштаба.

					Проект: Квартира 65 м²	**М 1:50**
	Лист	№ док.	Подпись	Дата	План покрытий пола	Стадия / Лист / Листов
Дизайнер	Кырлан А.С.			04.11.26		П / 40 / 83

Фрагмент 1. Санузел (пом. 6). Пол 600×1200, шов 2 мм, М 1:20

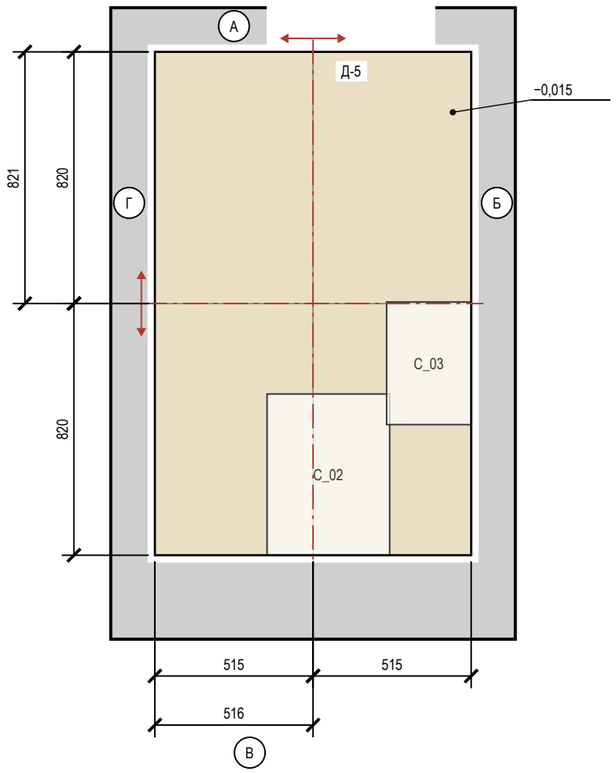

Фрагмент 2. Ванная (пом. 7). Пол 600×1200, шов 2 мм, М 1:20

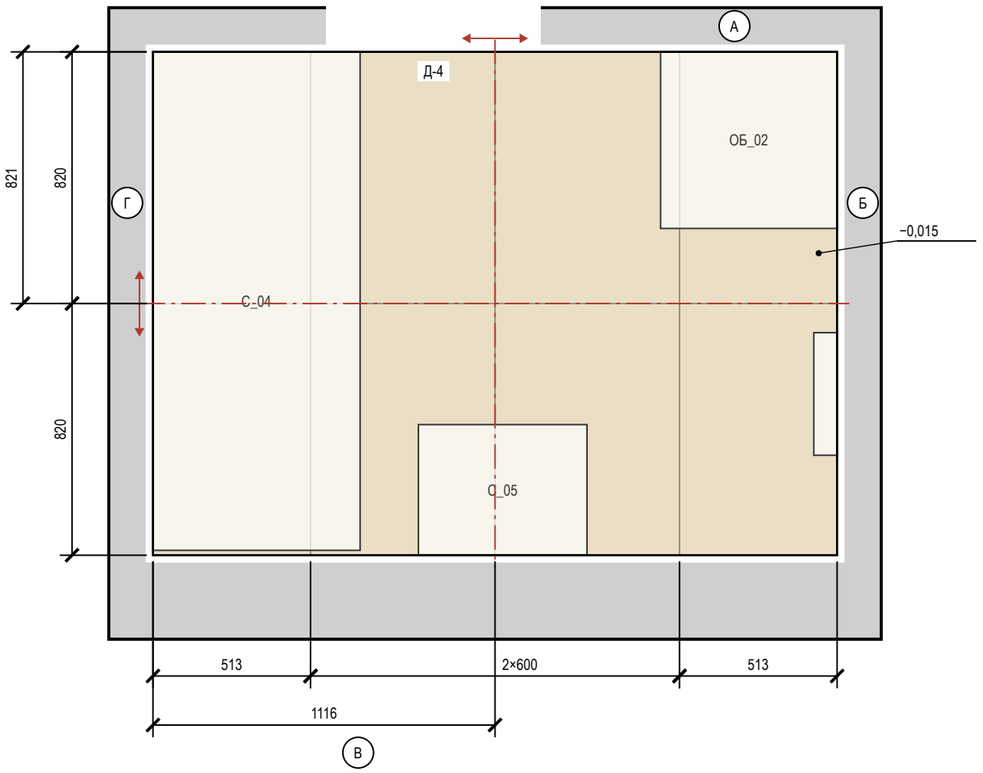

Условные обозначения

- плитка целая; тонкая линия — шов
- плитка с подрезкой (размер — на цепочке)
- ось старта; стрелки — направление укладки
- сантехприбор: габарит, высота по практике
- отметка чистого пола на полке выноски, м
- (А) обозначение стены А–Г (как на развёртках)

Ведомость плитки

Помещение, поверхность	Плитка, код	Формат	Шов	S, м²	Целых	Подр.	С запасом
Санузел, пол	SG501600R	600×1200	2	1,83	0	4	5
Санузел, стены А–Г	610010001195	1200×600	2	13,33	0	30	34
Ванная, пол	SG501600R	600×1200	2	3,85	0	8	9
Ванная, стены А–Г	610010001195	1200×600	2	19,29	0	40	44
Прихожая, пол	SG501600R	600×1200	2	4,15	0	8	9
Коридор, пол	SG501600R	600×1200	2	5,51	0	8	9
Итого 600×1200				**47,97**	**0**	**98**	**110**

Ведомость материалов


Материал	Класс, код	Норма расхода	Кол-во
Затирка	класс не задан	(a+b)/ab·шов·t·1,6	3,7 кг
Клей	C2 S1	1,5 кг/м²·мм, слой 5	45 кг (2 меш.)
Клей	C2	1,5 кг/м²·мм, слой 5	339 кг (14 меш.)
Гидроизоляция	обмазочная, 2 слоя: пол, стены по периметру и зоны замачивания	по ТУ	14,8 м²
Демпф. лента	по периметру пола из плитки		27,0 м

Примечания


1. Раскладка от чистовых размеров: стены санузлов теряют 10 + 5 + 9 = 24 мм на сторону (штукатурка, клей, плитка); подрезки — чистые, без шва.
2. Старт — от центра помещения (штрихпунктир, стрелки — направление укладки); размер старта — от чистовых стен Г и А.
3. Раскладка пола «Прихожая» и пола «Коридор» — на листе «Раскладка плитки. Прихожая. Коридор».
4. Калибр партии не задан — до укладки замерить (рабочий размер W, ГОСТ 13996-2019) и пересчитать подрезки.
5. Количество: целые по раскладке + по одной на подрезку, запас 10 %; один артикул — одна партия и тон. Исключены поддон, короб, проёмы и места за коробом; S — по чистым граням, как в ведомости отделки.
6. Клей C2 S1; C2 (ГОСТ Р 56387-2018), затирка класс не задан; расход — по ТУ выбранной марки.
7. Гидроизоляция: пол и стены 200 мм от ЧП; над ванной — до 2000 и 300 мм за борт (пом. 7) (см. развёртки); акт скрытых работ, пролив 24 ч.
8. Отметка чистого пола −0,015, порог 15 мм; стык с соседним покрытием — по оси полотна двери.

					Проект: Квартира 65 м²	**М 1:20**
	Лист	№ док.	Подпись	Дата		
Дизайнер	Кырлан А.С.			04.11.26	Раскладка плитки. Планы полов	Стадия / Лист / Листов
						П / 41 / 83

Фрагмент 1. Прихожая (пом. 4). Пол 600×1200, шов 2 мм, М 1:25

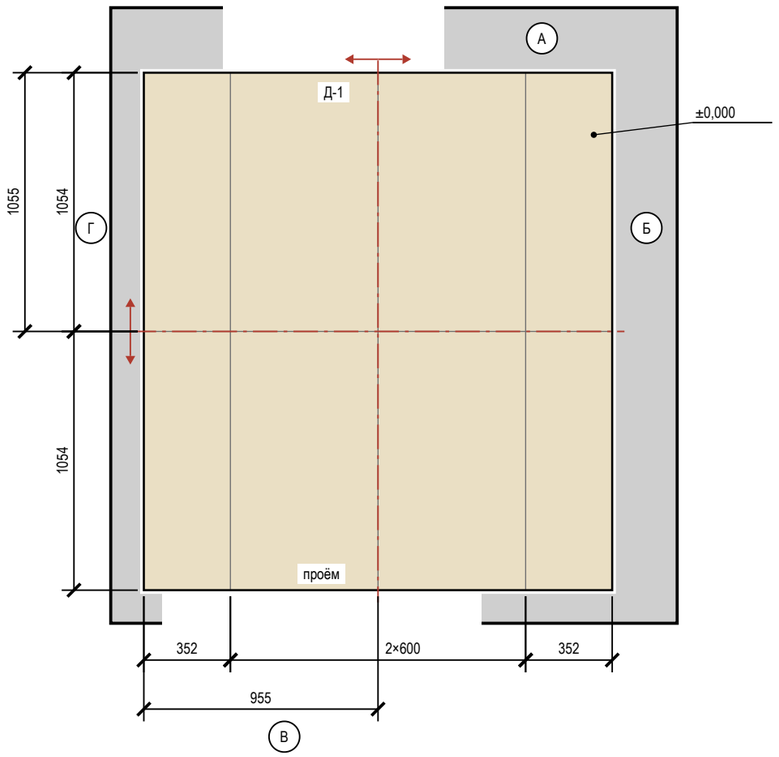

Фрагмент 2. Коридор (пом. 5). Пол 600×1200, шов 2 мм, М 1:25

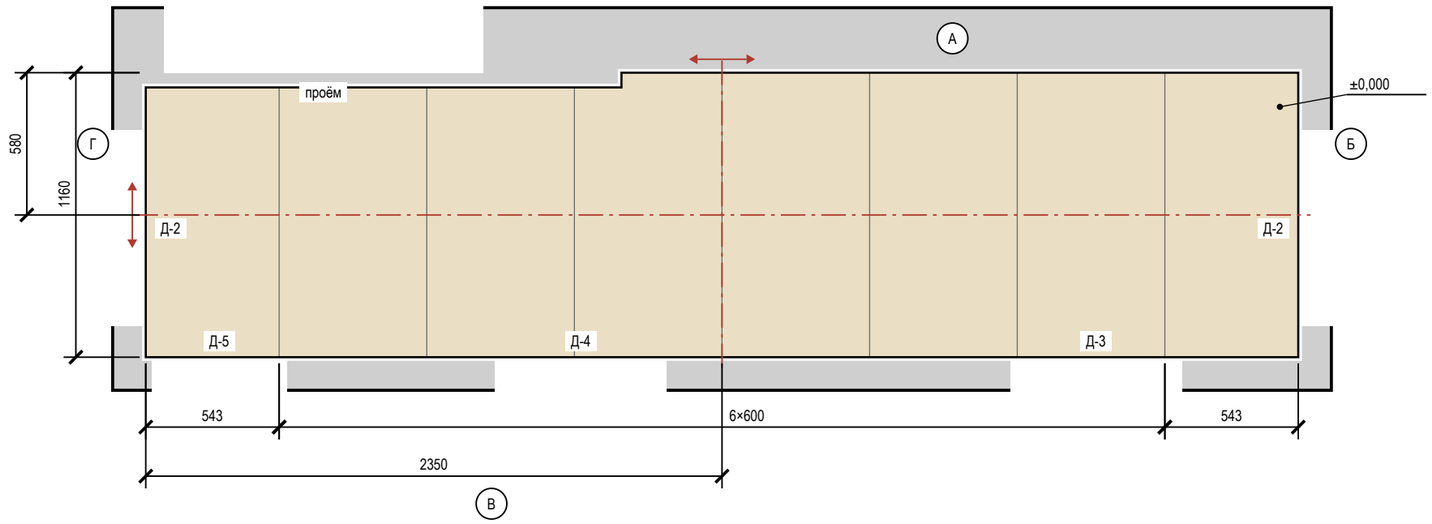

Условные обозначения

- плитка целая; тонкая линия — шов
- плитка с подрезкой (размер — на цепочке)
- ось старта; стрелки — направление укладки
- отметка чистого пола на полке выноски, м
- (А) обозначение стены А–Г (как на развёртках)

Подсчёт плитки


Поверхность	Формат	S, м²	Целых	Подр.	С запасом
Прихожая, пол	600×1200	4,15	0	8	9
Коридор, пол	600×1200	5,51	0	8	9

Примечания

1. Прихожая: керамогранит 600×1200, длинная сторона — вдоль стен Б и Г, шов 2 мм, прямая раскладка от центра. Стены окрашены: раскладка от чистового контура минус штукатурка и шпаклёвка 15 мм на сторону (принято); подрезки 352 / 1054 мм, срез — под плинтус.
2. Прихожая: деформационный зазор по периметру 8–10 мм под плинтусом; в проёмах — стык с соседним покрытием по оси полотна двери. Клей С2, затирка класс не задан.
3. Коридор: керамогранит 600×1200, длинная сторона — вдоль стен Б и Г, шов 2 мм, прямая раскладка от центра. Стены окрашены: раскладка от чистового контура минус штукатурка и шпаклёвка 15 мм на сторону (принято); подрезки 543 / 1160 мм, срез — под плинтус.
4. Коридор: деформационный зазор по периметру 8–10 мм под плинтусом; в проёмах — стык с соседним покрытием по оси полотна двери. Клей С2, затирка класс не задан.
5. Клей, затирка и итог по форматам — в ведомостях листа «Раскладка плитки. Планы полов».

					Проект: Квартира 65 м²	М 1:25
	Лист	№ док.	Подпись	Дата		
Дизайнер	Кырлан А.С.			04.11.26	Раскладка плитки. Прихожая. Коридор	Стадия: П; Лист: 42; Листов: 83

Развёртка стены А

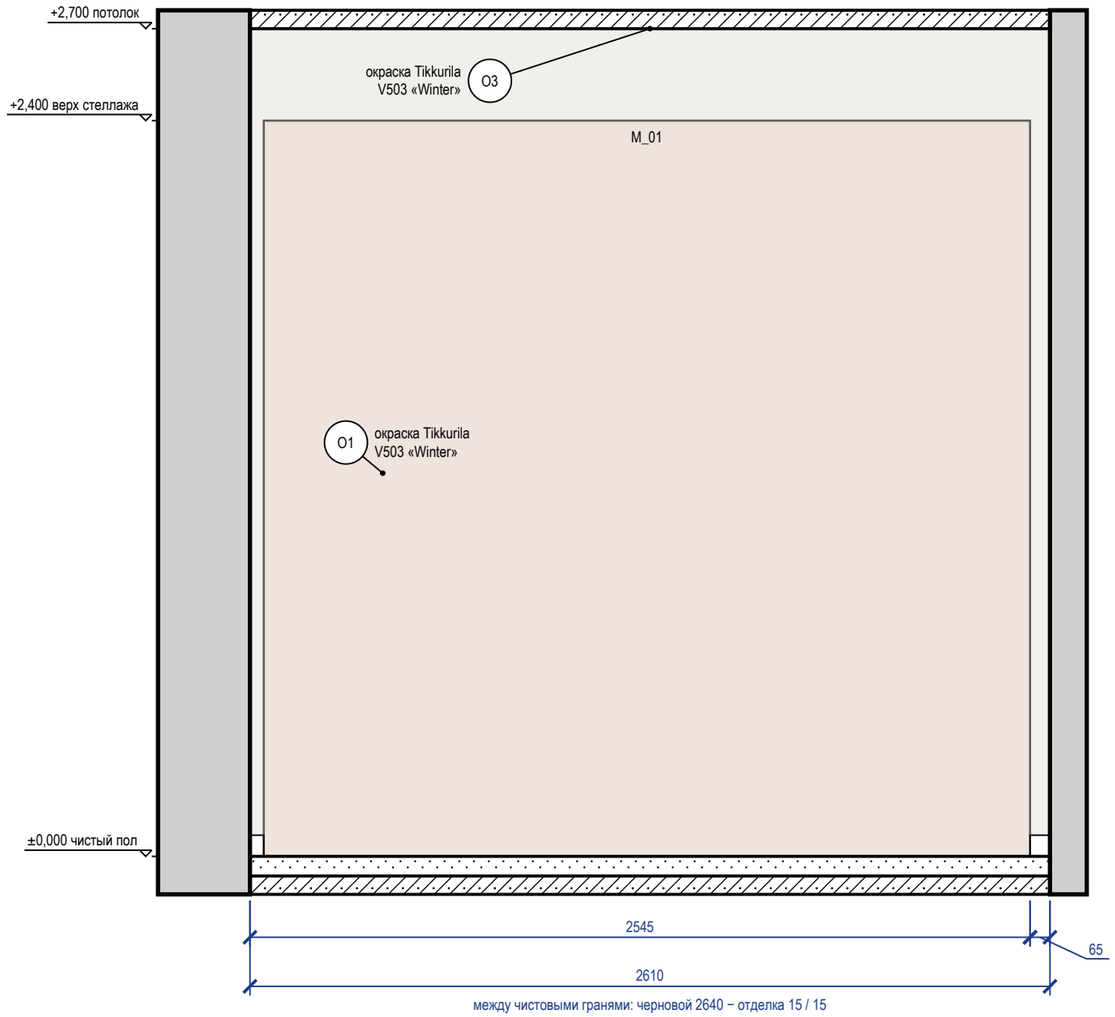

Развёртка стены Б


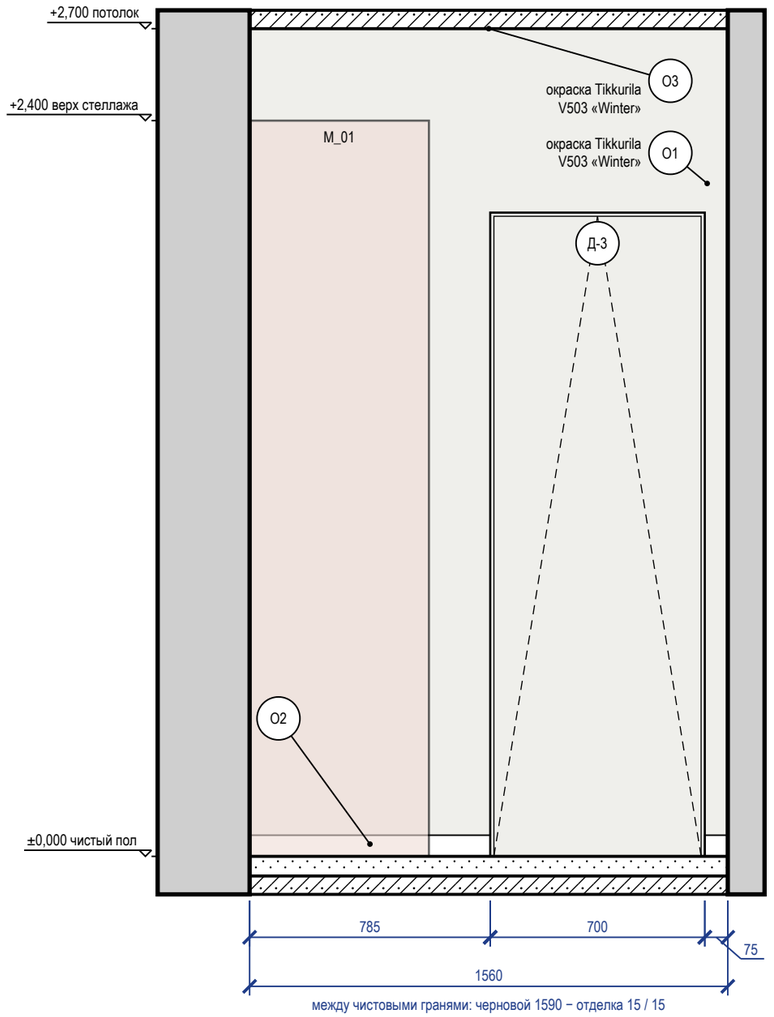


Схема развёрток (М 1:100)

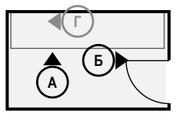

Ведомость отделки (на листе)

Марка	Поверхность	Материал, изделие	Цвет, код	Кол.
О1	стены	окраска, Tikkurila Harmony, матовая, подготовка Q3	Tikkurila V503 «Winter»	9,8 м²
О2	плинтус	плинтус МДФ, Orac Decor Contour (Luxxus), h 69 мм, SX165	Tikkurila V503 «Winter»	1 м
О3	потолок	окраска, Tikkurila Anti-Reflex 2, глубокоматовая, подготовка Q3	Tikkurila V503 «Winter»	4,2 м²

Примечания

1. Размеры — в мм от чистовых поверхностей стен; условные обозначения и общие указания — лист 3.
2. Двери скрытого монтажа — полотно в плоскости стены, отделка стены по полотну, плинтус прерывается у короба (узел — на листе узлов).

					Проект: Квартира 65 м² — М 1:20
	Лист	№ док.	Подпись	Дата	Развёртки стен А, Б. Гардеробная (пом. 1)
Дизайнер	Кырлан А.С.			04.11.26	Стадия: П; Лист: 43; Листов: 83

Развёртка стены Г


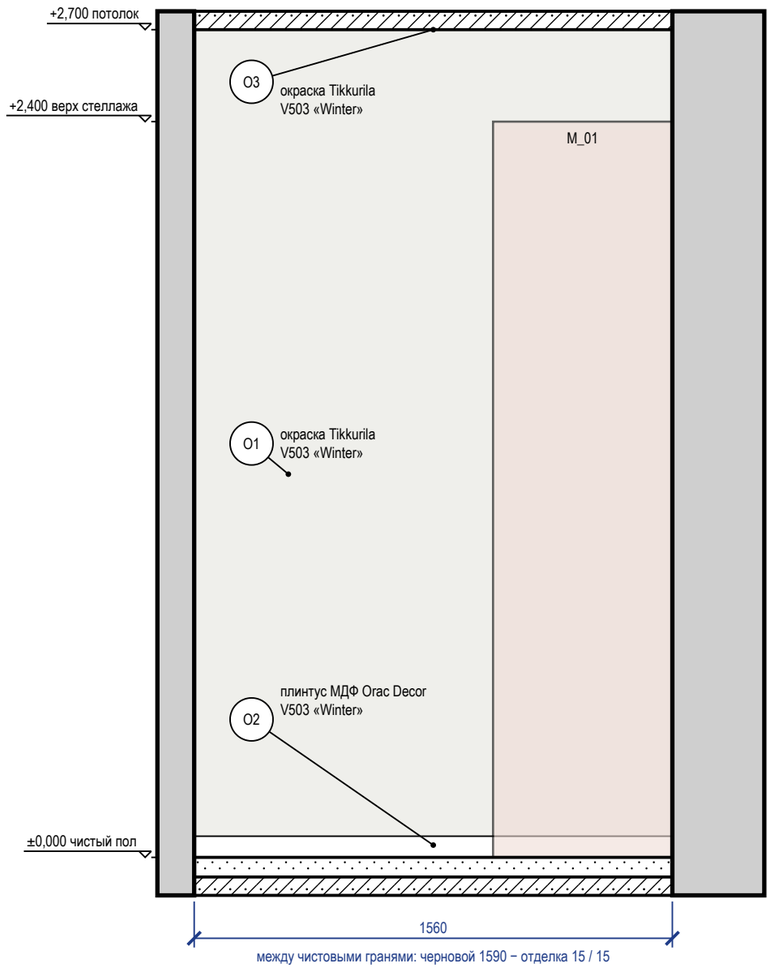


Схема развёрток (М 1:100)

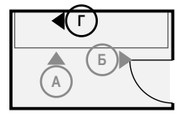

Ведомость отделки (на листе)

Марка	Поверхность	Материал, изделие	Цвет, код	Кол.
О1	стены	окраска, Tikkurila Harmony, матовая, подготовка Q3	Tikkurila V503 «Winter»	4,2 м²
О2	плинтус	плинтус МДФ, Orac Decor Contour (Luxxus), h 69 мм, SX165	Tikkurila V503 «Winter»	1,6 м
О3	потолок	окраска, Tikkurila Anti-Reflex 2, глубокоматовая, подготовка Q3	Tikkurila V503 «Winter»	4,2 м²

Примечания

1. Размеры — в мм от чистовых поверхностей стен; условные обозначения и общие указания — лист 3.

					Проект: Квартира 65 м²	М 1:20
	Лист	№ док.	Подпись	Дата		
Дизайнер	Кырлан А.С.			04.11.26	Развёртка стены Г. Гардеробная (пом. 1)	
					Стадия: П	Лист: 44 / Листов: 83

Развёртка стены А


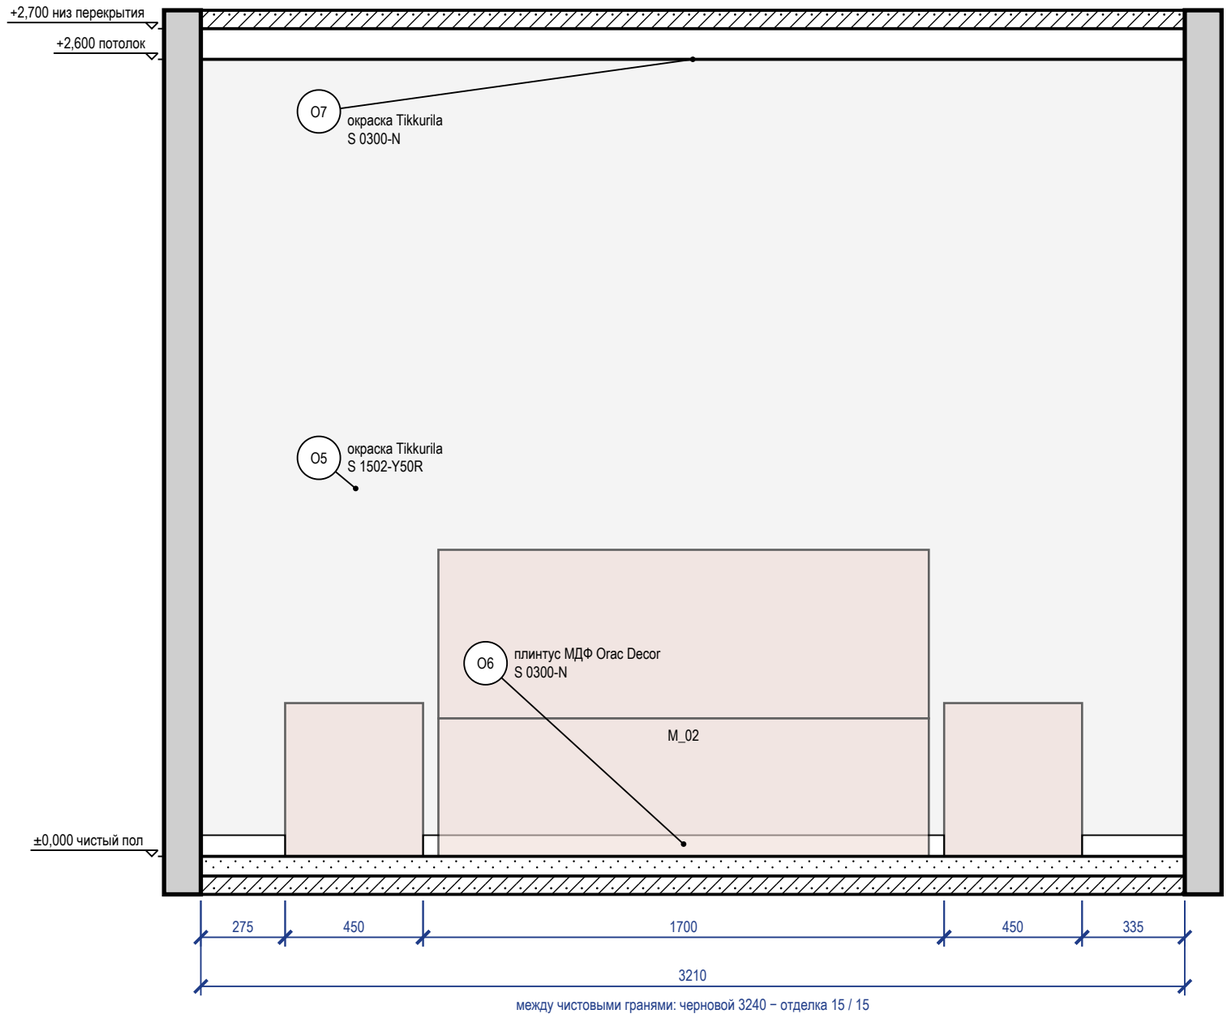


Схема развёрток (М 1:100)

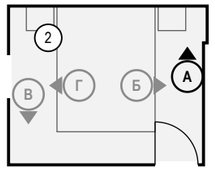

Ведомость отделки (на листе)

Марка	Поверхность	Материал, изделие	Цвет, код	Кол.
О5	стены	окраска, Tikkurila, глубокоматовая, подготовка Q3	NCS S 1502-Y50R	8,3 м²
О6	плинтус	плинтус МДФ, Orac Decor Contour (Luxxus), h 69 мм, SX165, шелковисто-матовая	NCS S 0300-N	2,3 м
О7	потолок	окраска, Tikkurila, глубокоматовая	NCS S 0300-N	8,3 м²

Примечания

1. Размеры — в мм от чистовых поверхностей стен; условные обозначения и общие указания — лист 3.
2. Стена А показана двумя видами: здесь — архитектурная развёртка (мебель, отделка, проёмы, высоты), электроточки и выводы ВК с привязками и таблицей — на листе 46 («Привязки»).

					Проект: Квартира 65 м²	М 1:20
	Лист	№ док.	Подпись	Дата		
Дизайнер	Кырлан А.С.			04.11.26	Развёртка стены А. Спальня (пом. 2)	Стадия: П; Лист: 45; Листов: 83

Развёртка стены А: электроточки и выводы

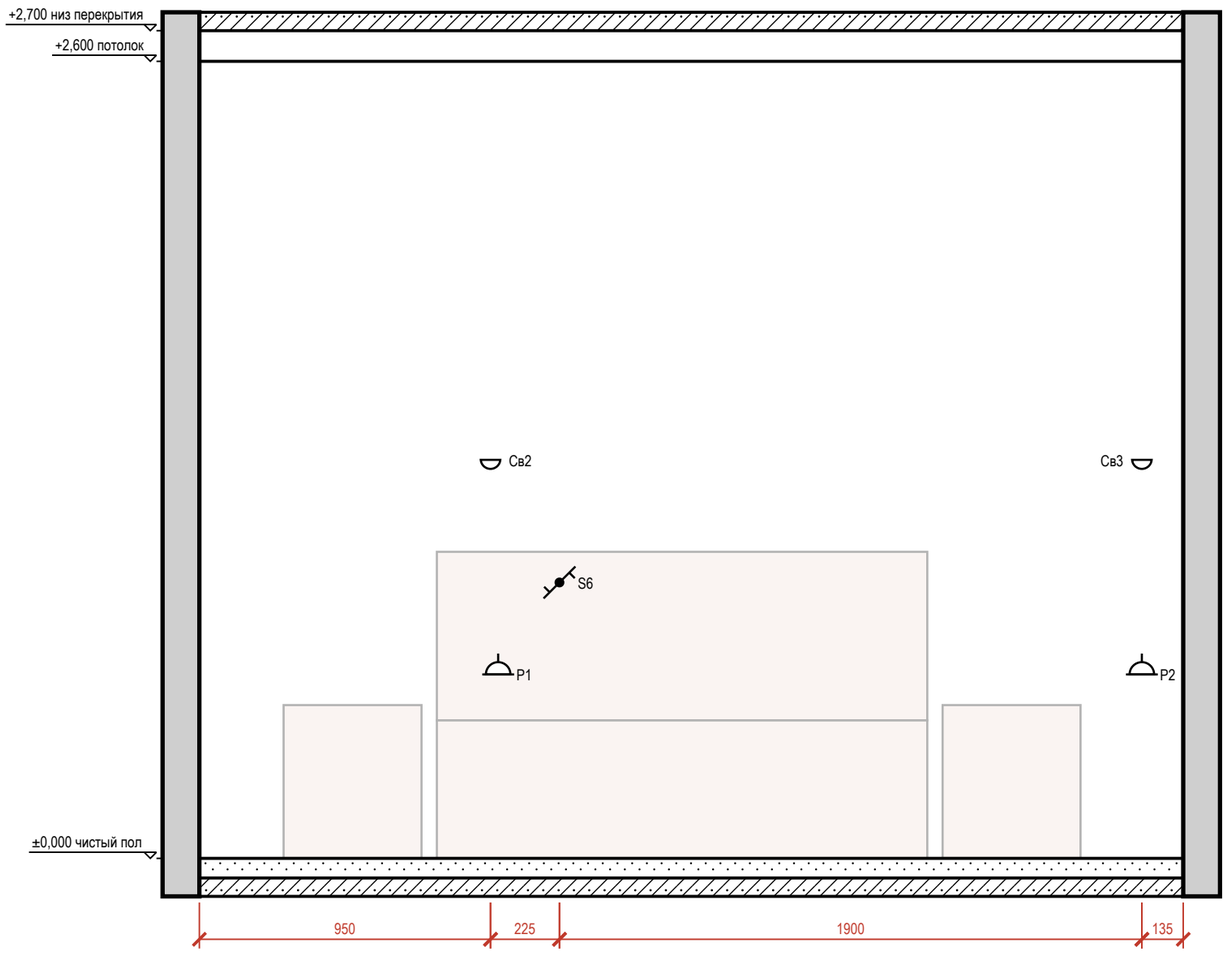



Таблица привязок электроточек и выводов

Марка	Назначение	От угла, мм	H от пола, мм	Примечание
Св2	светильник настенный	950	1300	гр. 1
P1	розетка	975	600	гр. 4
S6	выключатель	1175	900	гр. 1
P2	розетка	3075	600	гр. 4
Св3	светильник настенный	3075	1300	гр. 1

Условные обозначения

- розетка с заземляющим контактом; у знака — марка, ×N постов в рамке, гр. — группа щита, H — высота оси, мм
- выключатель одноклавишный
- выключатель с проходной или перекрёстной клавишей (обратный флажок); тип клавиши — в подписи
- светильник настенный (бра), H — высота оси
- привязки точек и выводов от угла и от пола, мм
- марка развёртки: буква стены, стрелка — взгляд

Схема развёрток (М 1:50)

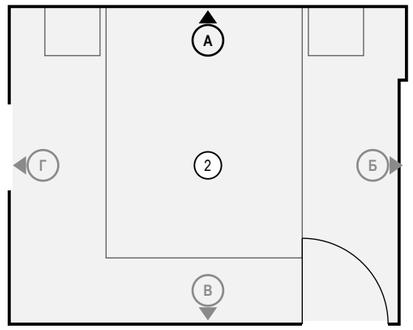


Примечания

1. Вид «Привязки» стены А — электроточки и выводы ВК; архитектурная развёртка (мебель, отделка, проёмы, высоты) — на листе 45. Мебель и приборы — подложкой для ориентира; их марки и обозначения мебели, проёмов и стен — там же.
2. Привязки — в мм: по горизонтали от левого чистового угла стены до оси изделия, H — от чистого пола до оси; все точки — в таблице привязок. Красная цепочка — привязки по осям; точки ближе 120 мм одна к другой в цепочку не дробятся — их привязки только в таблице.
3. У знака — марка электроточки (P — розетка, S — выключатель, Св — светильник, ЭВ — вывод кабеля); условные обозначения и общие указания — лист 3.


					Проект: Квартира 65 м² — **М 1:20**
	Лист	№ док.	Подпись	Дата	Привязки электроточек, стена А. Спальня (пом. 2)
Дизайнер	Кырлан А.С.			04.11.26	Стадия: П; Лист: 46; Листов: 83

Развёртка стены Б

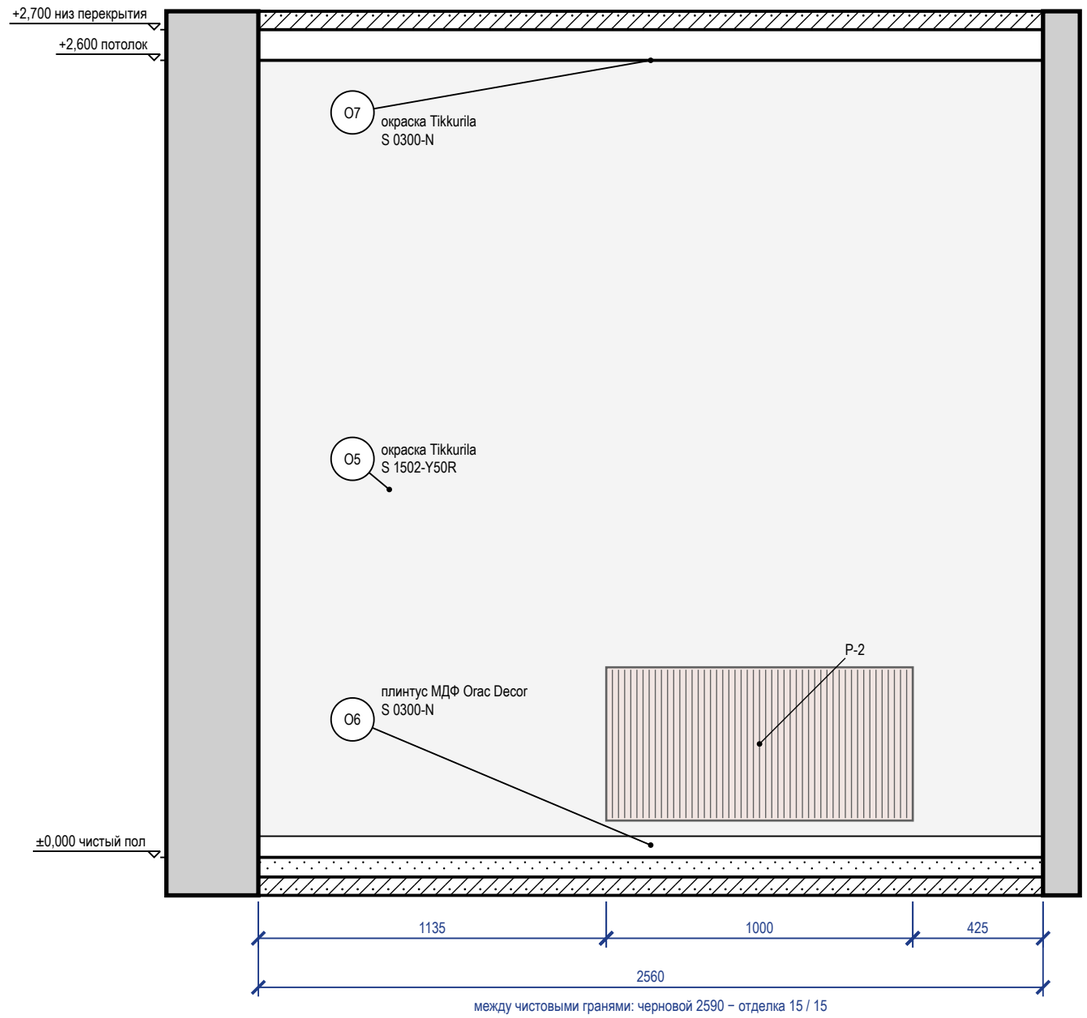


между чистовыми гранями: черновой 2590 − отделка 15 / 15

Развёртка стены Г

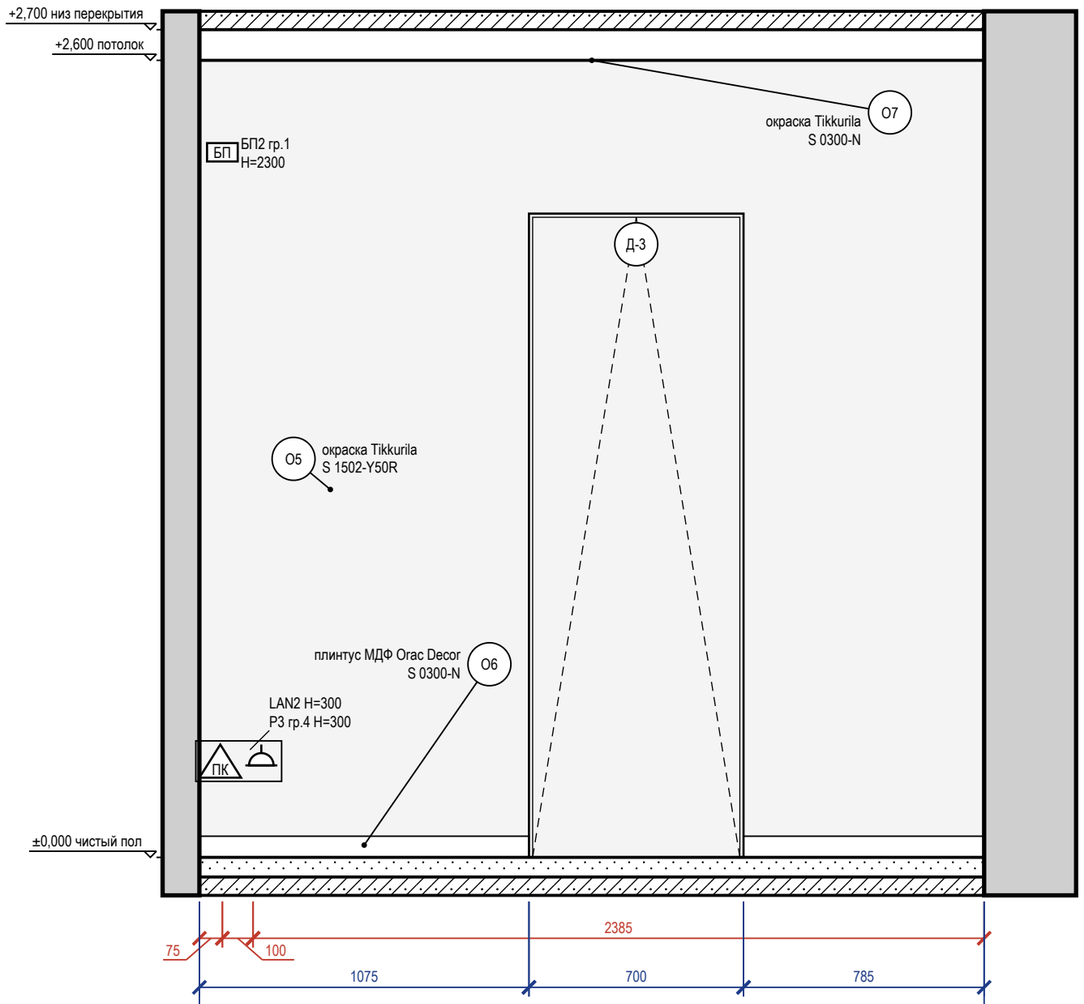

между чистовыми гранями: черновой 2590 − отделка 15 / 15

Схема развёрток (М 1:100)

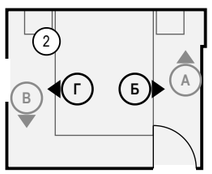

Ведомость отделки (на листе)

Марка	Поверхность	Материал, изделие	Цвет, код	Кол.
О5	стены	окраска, Tikkurila, глубокоматовая, подготовка Q3	NCS S 1502-Y50R	11,8 м²
О6	плинтус	плинтус МДФ, Orac Decor Contour (Luxxus), h 69 мм, SX165, шелковисто-матовая	NCS S 0300-N	4,4 м
О7	потолок	окраска, Tikkurila, глубокоматовая	NCS S 0300-N	8,3 м²

Примечания

1. Размеры — в мм от чистовых поверхностей стен; условные обозначения и общие указания — лист 3.
2. Двери скрытого монтажа — полотно в плоскости стены, отделка стены по полотну, плинтус прерывается у короба (узел — на листе узлов).

					Проект: Квартира 65 м²	М 1:20
	Лист	№ док.	Подпись	Дата	Развёртки стен Б, Г. Спальня (пом. 2)	Стадия: П; Лист: 47; Листов: 83
Дизайнер	Кырлан А.С.			04.11.26		

выпуск 04.11.2026 № 84932ed378 · стр. 47 из 83

Развёртка стены В


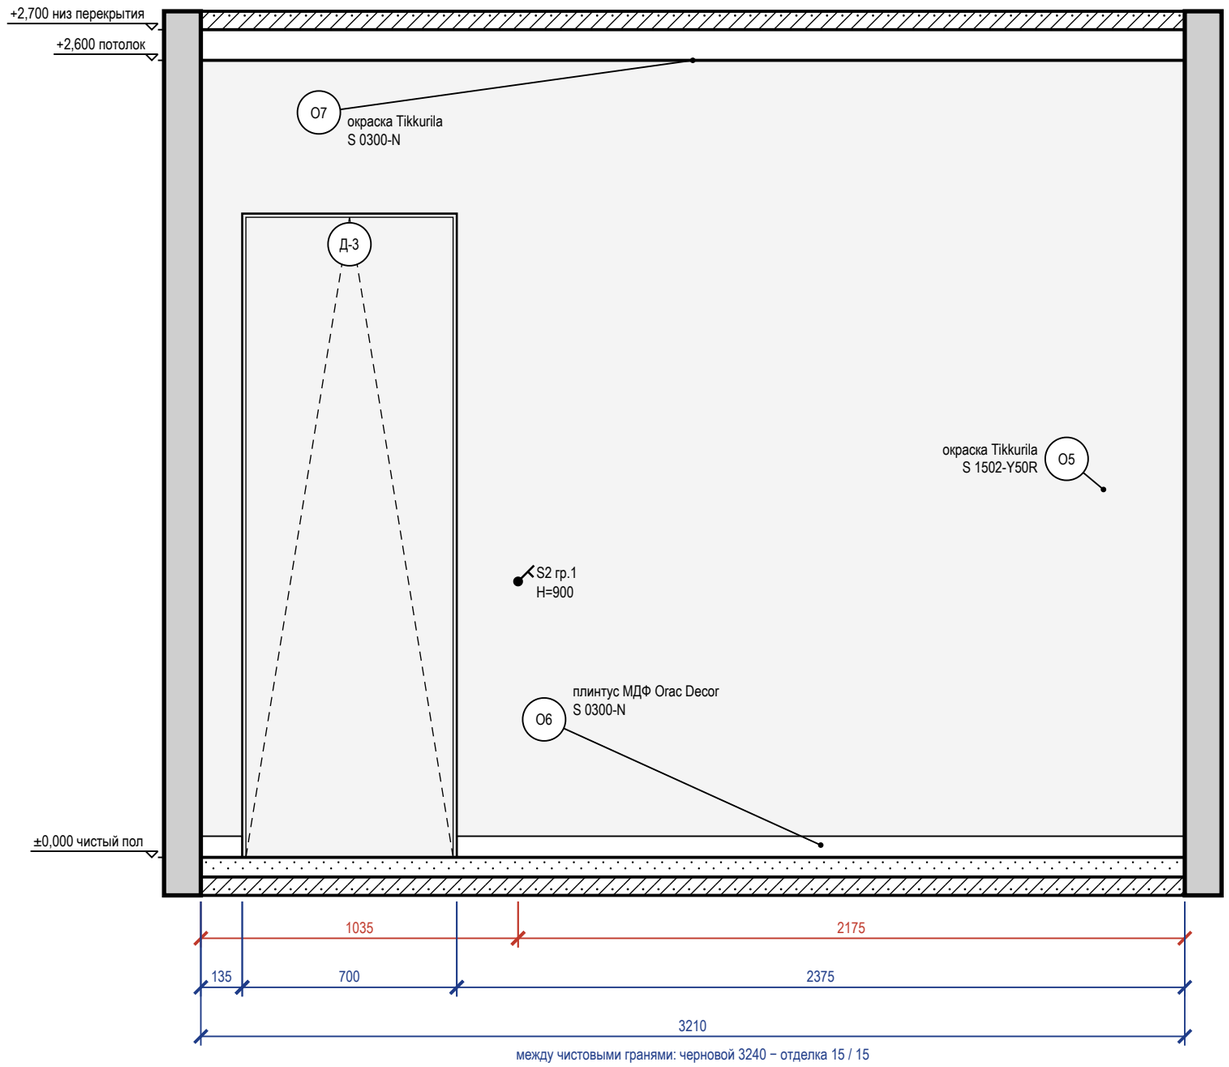


Схема развёрток (М 1:100)

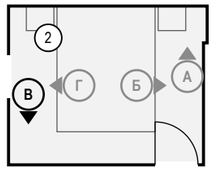


Ведомость отделки (на листе)

Марка	Поверхность	Материал, изделие	Цвет, код	Кол.
О5	стены	окраска, Tikkurila, глубокоматовая, подготовка Q3	NCS S 1502-Y50R	6,9 м²
О6	плинтус	плинтус МДФ, Orac Decor Contour (Luxxus), h 69 мм, SX165, шелковисто-матовая	NCS S 0300-N	2,5 м
О7	потолок	окраска, Tikkurila, глубокоматовая	NCS S 0300-N	8,3 м²

5 **Плинтус МДФ 69×16 мм у окрашенной стены по доске (ламинату) (М 1:10)**

Узел 5 — лист С6

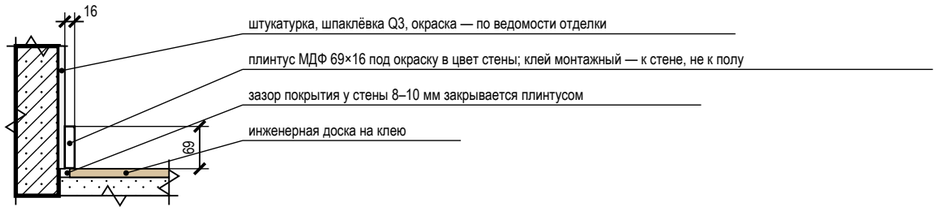


Примечания

1. Размеры — в мм от чистовых поверхностей стен; условные обозначения и общие указания — лист 3.
2. Двери скрытого монтажа — полотно в плоскости стены, отделка стены по полотну, плинтус прерывается у короба (узел — на листе узлов).


					Проект: Квартира 65 м²	М 1:20
	Лист	№ док.	Подпись	Дата	Развёртка стены В. Спальня (пом. 2)	Стадия / Лист / Листов
Дизайнер	Кырлан А.С.			04.11.26		П / 48 / 83

Развёртка стены В

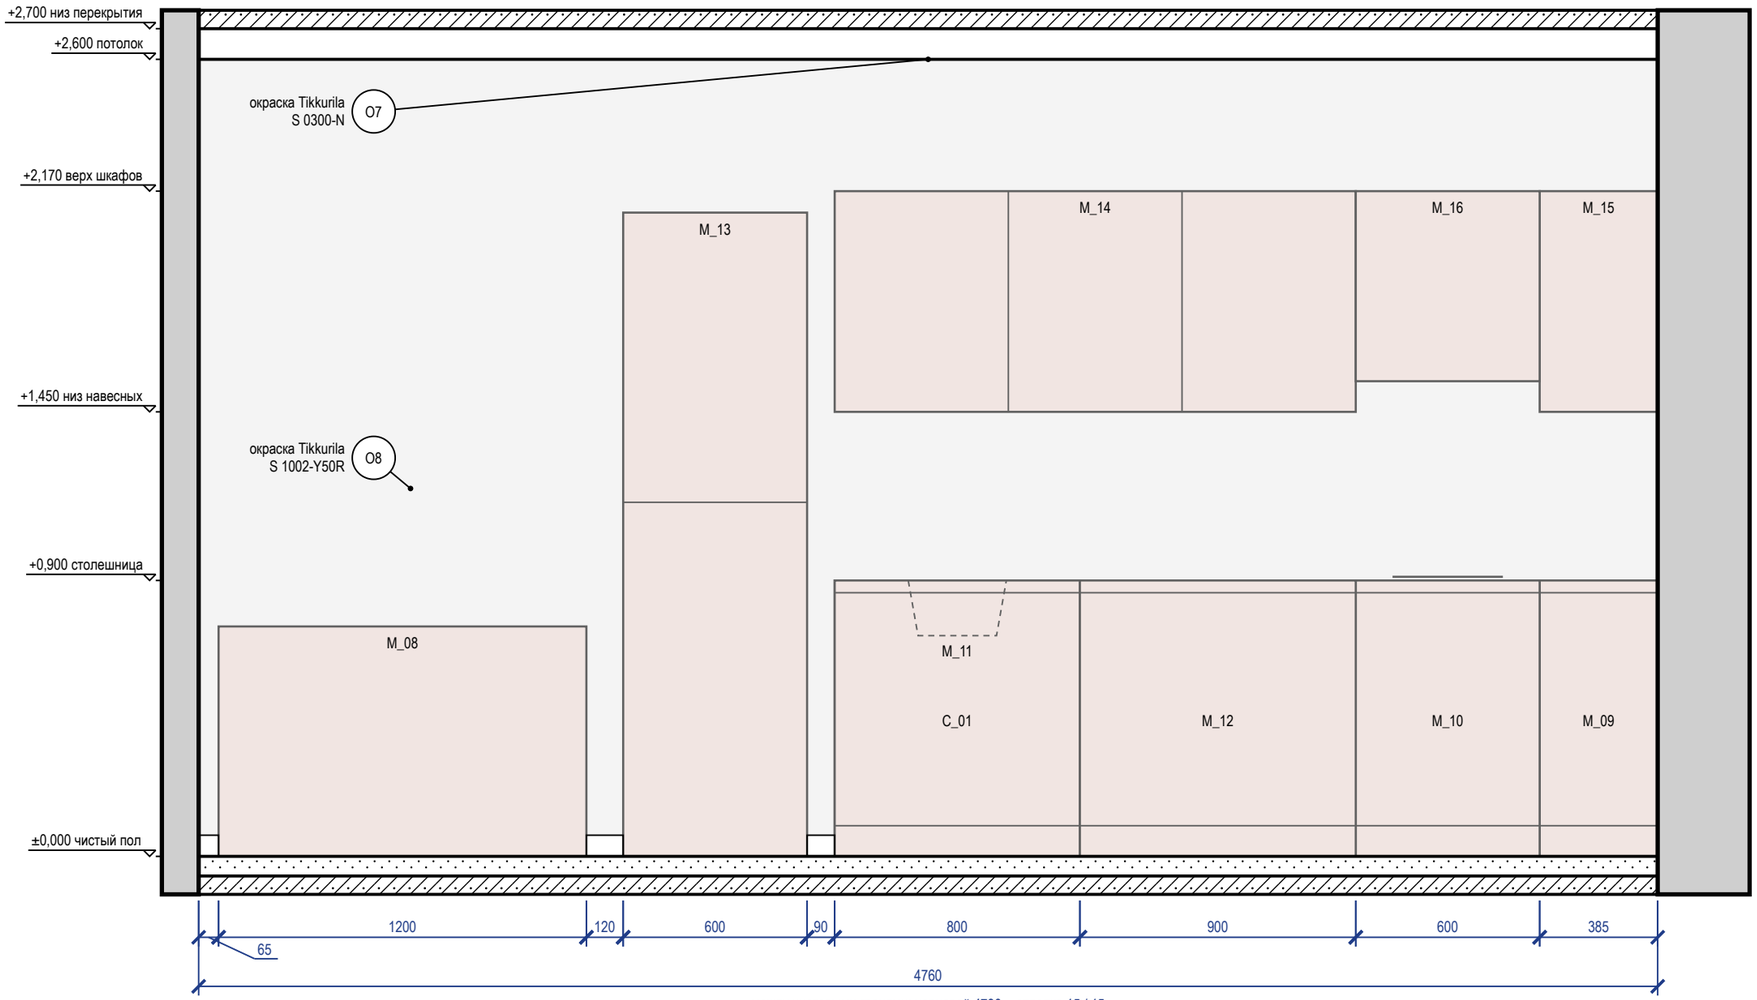

между чистовыми гранями: черновой 4790 − отделка 15 / 15

Схема развёрток (М 1:100)

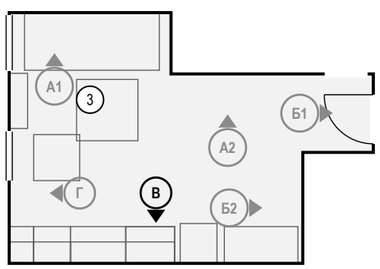

Ведомость отделки (на листе)

Марка	Поверхность	Материал, изделие	Цвет, код	Кол.
О6	плинтус	плинтус МДФ, Orac Decor Contour (Luxxus), h 69 мм, SX165, шелковисто-матовая	NCS S 0300-N	0,3 м
О7	потолок	окраска, Tikkurila, глубокоматовая	NCS S 0300-N	18,9 м²
О8	стены	окраска, Tikkurila, шелковисто-матовая, подготовка Q3	NCS S 1002-Y50R	12,4 м²


Примечания

1. Размеры — в мм от чистовых поверхностей стен; условные обозначения и общие указания — лист 3.
2. Стена В показана двумя видами: здесь — архитектурная развёртка (мебель, отделка, проёмы, высоты), электроточки и выводы ВК с привязками и таблицей — на листе 50 («Привязки»).

					Проект: Квартира 65 м²	М 1:20
	Лист	№ док.	Подпись	Дата	Развёртка стены В. Кухня-гостиная (пом. 3), кухонный фронт	Стадия: П; Лист: 49; Листов: 83
Дизайнер	Кырлан А.С.			04.11.26		

выпуск 04.11.2026 № 84932ed378 · стр. 49 из 83

Развёртка стены В: электроточки и выводы

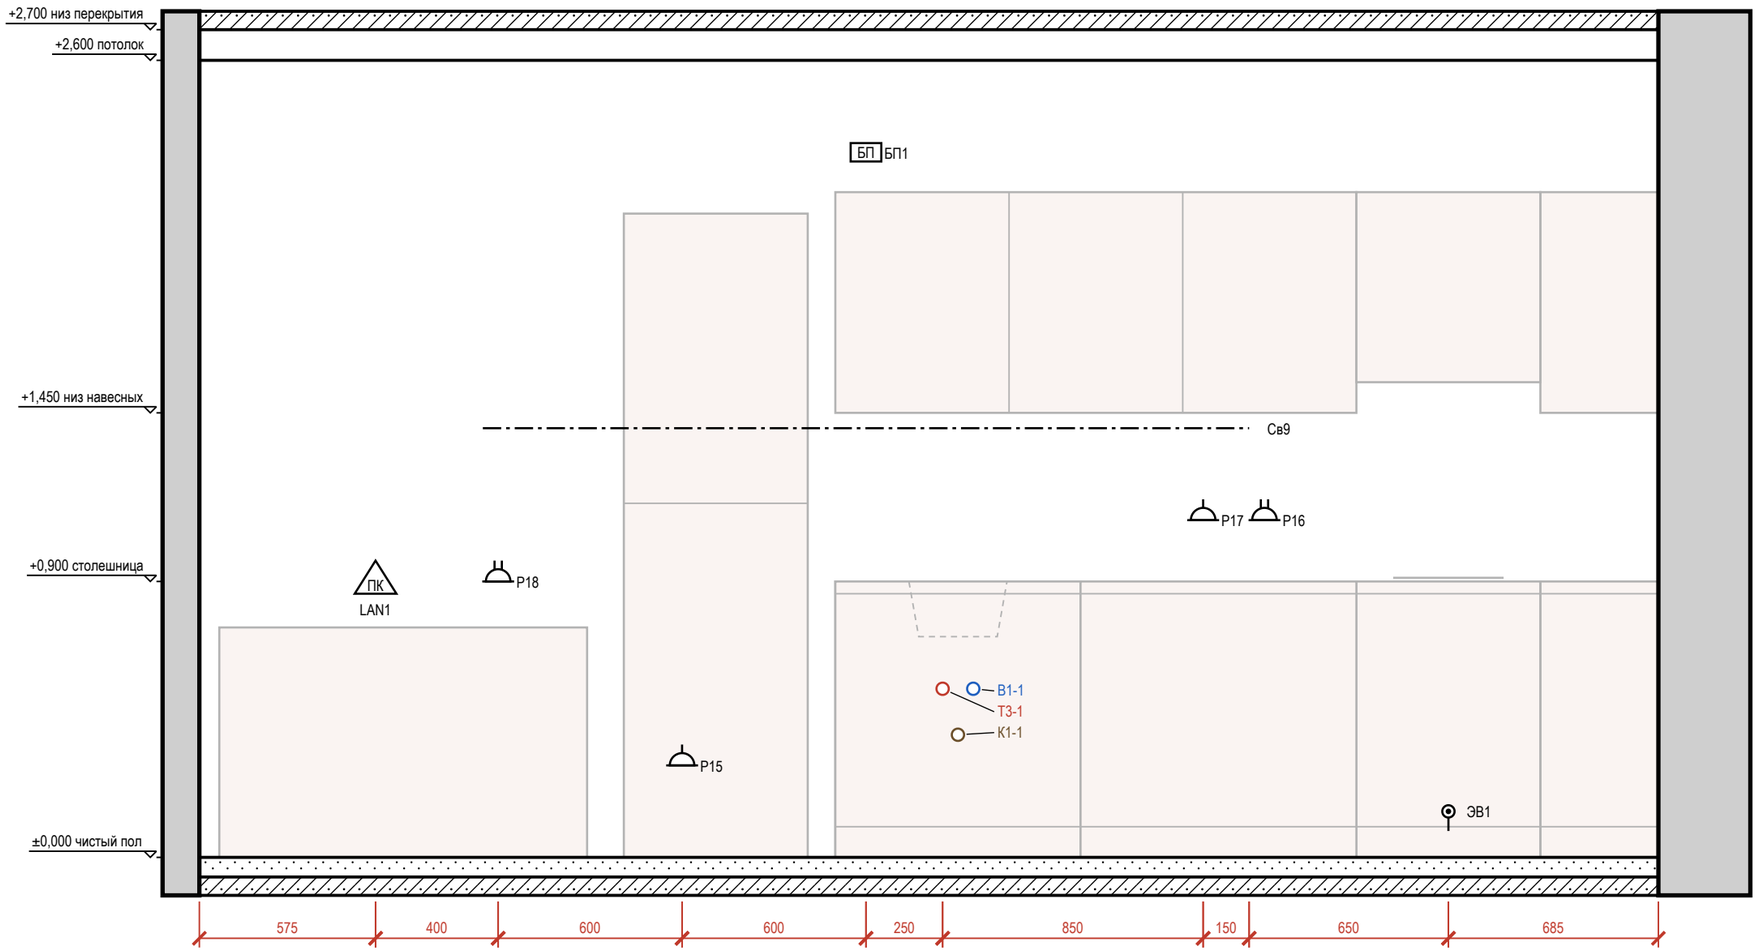

Условные обозначения

- розетка с заземляющим контактом; у знака — марка, ×N постов в рамке, гр. — группа щита, Н — высота оси, мм
- вывод кабеля для подключения прибора (без розетки), марка ЭВ
- светодиодная лента в профиле / в карнизе короба
- БП — блок питания LED, с доступом (люк от 100×100 мм)
- ПК — розетка компьютерная RJ45
- вывод В1 (код — в ведомости привязок)
- вывод Т3 (код — в ведомости привязок)
- вывод К1 (код — в ведомости привязок)
- привязки точек и выводов от угла и от пола, мм
- А — марка развёртки: буква стены, стрелка — взгляд

Схема развёрток (М 1:100)

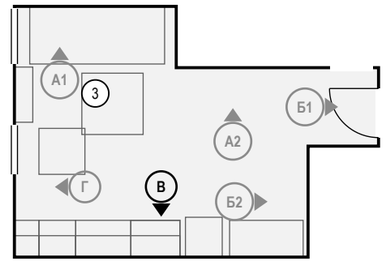


Таблица привязок электроточек и выводов

Марка	Назначение	От угла, мм	Н от пола, мм	Примечание
LAN1	розетка RJ45: рабочее место	575	900	
Р18	розетка: рабочее место	975	900	рамка 2 поста, гр. 4
Р15	розетка: холодильник	1575	300	гр. 2
БП1	блок питания LED	2175	2300	гр. 1
Т3-1	горячая вода — мойка кухонная	2425	550	межос. 100
К1-1	канализация — мойка кухонная	2475	400	Ø50

Марка	Назначение	От угла, мм	Н от пола, мм	Примечание
В1-1	холодная вода — мойка кухонная	2525	550	межос. 100
Р17	розетка: рабочая зона	3275	1100	гр. 2
Св9	светильник настенный	3425	1400	гр. 1, лента 925–3425 от угла
Р16	розетка: рабочая зона	3475	1100	рамка 2 поста, гр. 2
ЭВ1	вывод кабеля: варочная панель	4075	150	гр. 3

Примечания

1. Вид «Привязки» стены В — электроточки и выводы ВК; архитектурная развёртка (мебель, отделка, проёмы, высоты) — на листе 49. Мебель и приборы — подложкой для ориентира; их марки и обозначения мебели, проёмов и стен — там же.
2. Привязки — в мм: по горизонтали от левого чистового угла стены до оси изделия, Н — от чистого пола до оси; все точки — в таблице привязок. Красная цепочка — привязки по осям; точки ближе 120 мм одна к другой в цепочку не дробятся — их привязки только в таблице.
3. У знака — марка электроточки (Р — розетка, S — выключатель, Св — светильник, ЭВ — вывод кабеля); условные обозначения и общие указания — лист 3.
4. Коды выводов ВК: В1 — холодная вода, Т3 — горячая вода, К1 — канализация; номер после дефиса — номер вывода на листе выводов сантехники.
5. Выводы кухонной техники — по утверждённому проекту кухни: привязки выводов даются от осей модулей гарнитура.

					Проект: Квартира 65 м²	М 1:20
	Лист	№ док.	Подпись	Дата	Привязки электроточек и выводов ВК, стена В. Кухня-гостиная (пом. 3)	
Дизайнер	Кырлан А.С.			04.11.26		

Стадия	Лист	Листов
П	50	83

Развёртка стены Г


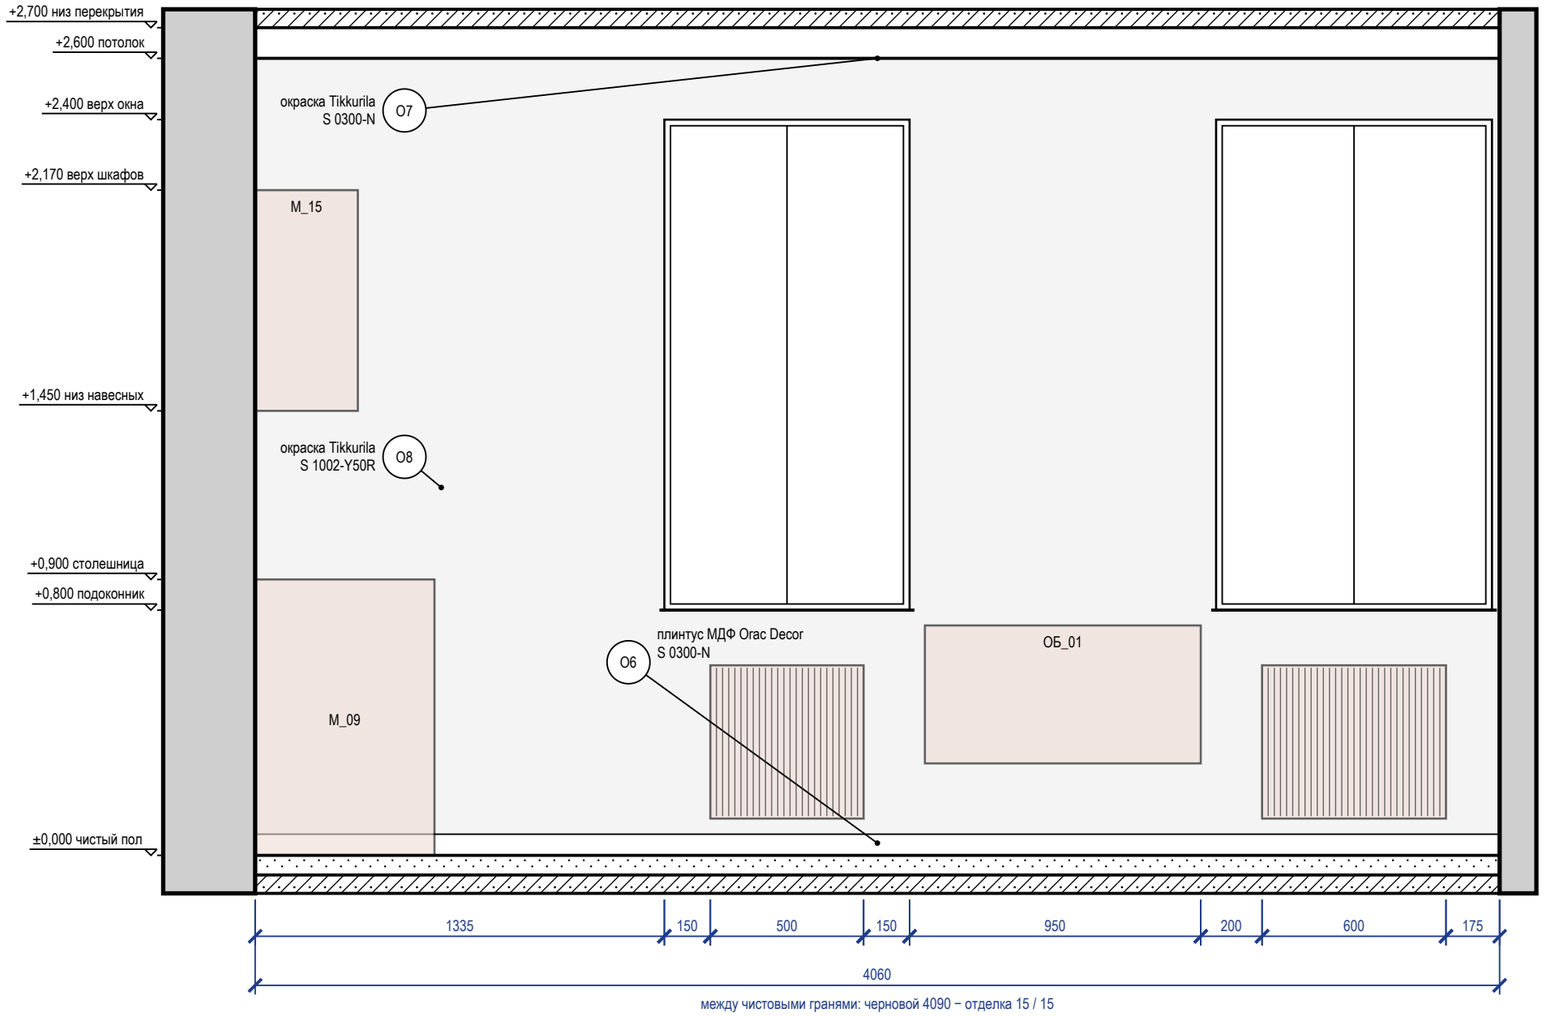


Схема развёрток (М 1:100)

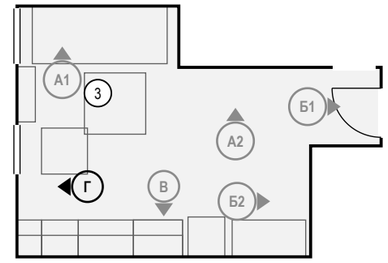

Ведомость отделки (на листе)

Марка	Поверхность	Материал, изделие	Цвет, код	Кол.
О6	плинтус	плинтус МДФ, Orac Decor Contour (Luxxus), h 69 мм, SX165, шелковисто-матовая	NCS S 0300-N	4,1 м
О7	потолок	окраска, Tikkurila, глубокоматовая	NCS S 0300-N	18,9 м²
О8	стены	окраска, Tikkurila, шелковисто-матовая, подготовка Q3	NCS S 1002-Y50R	7,8 м²

Примечания

1. Размеры — в мм от чистовых поверхностей стен; условные обозначения и общие указания — лист 3.
2. Стена Г показана двумя видами: здесь — архитектурная развёртка (мебель, отделка, проёмы, высоты), электроточки и выводы ВК с привязками и таблицей — на листе 52 («Привязки»).

					Проект: Квартира 65 м²	М 1:20
	Лист	№ док.	Подпись	Дата		
Дизайнер	Кырлан А.С.			04.11.26	Развёртка стены Г. Кухня-гостиная (пом. 3), кухонный фронт	Стадия: П; Лист: 51; Листов: 83

Развёртка стены Г: электроточки и выводы

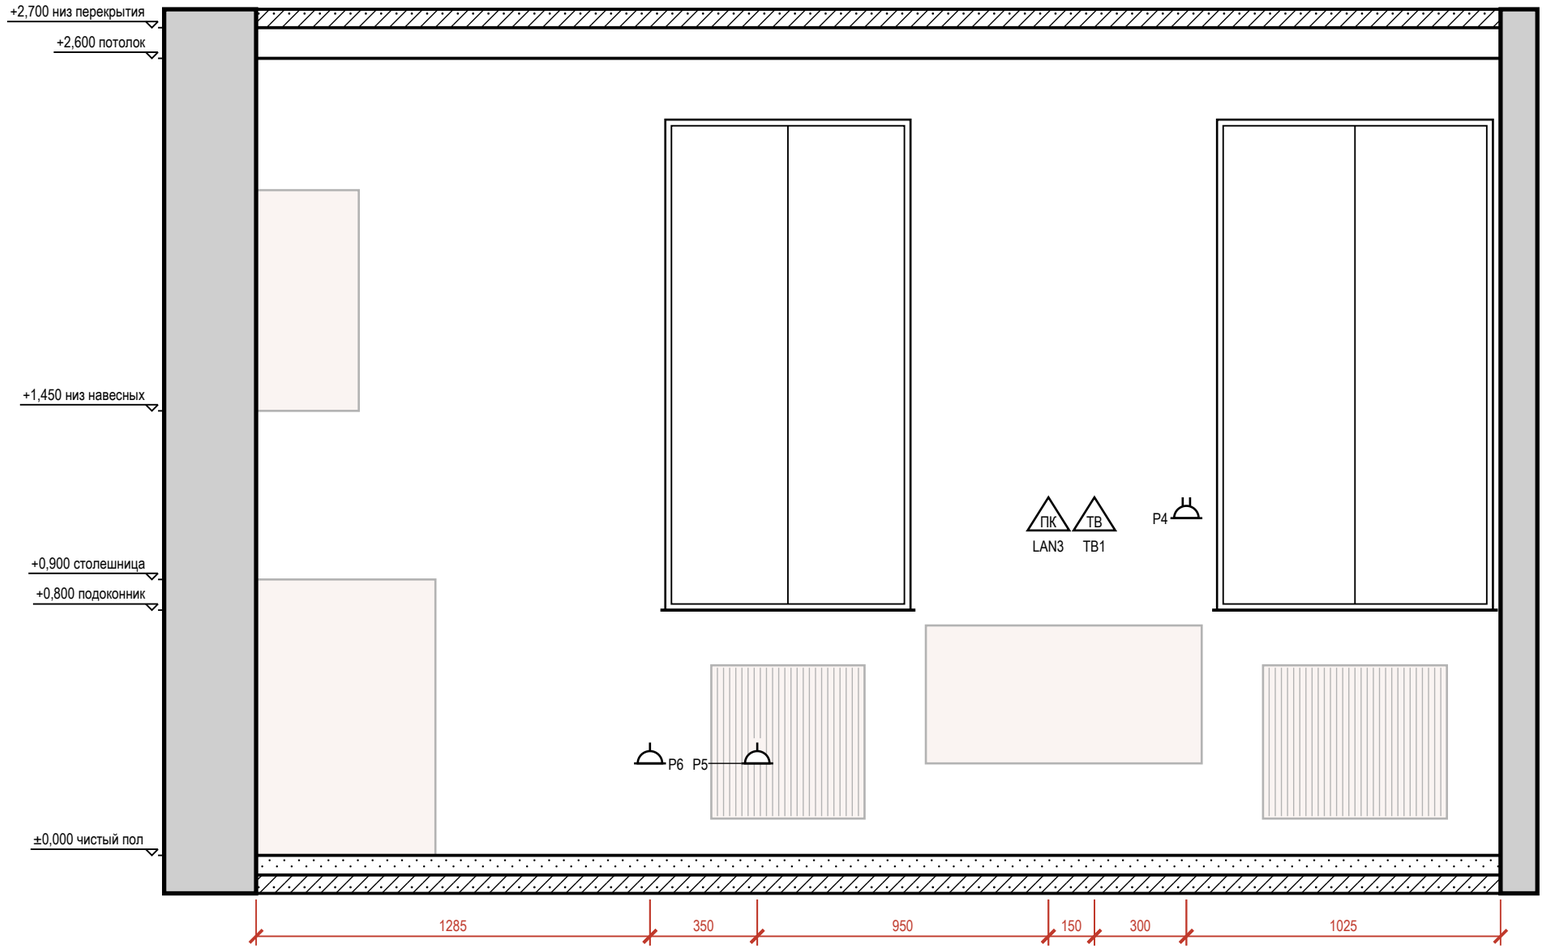



Таблица привязок электроточек и выводов

Марка	Назначение	От угла, мм	Н от пола, мм	Примечание
Р6	розетка: торшер у кресла M_06	1285	300	гр. 4
Р5	розетка: обеденная зона	1635	300	гр. 4
LAN3	розетка RJ45: Smart TV	2585	1100	
ТВ1	розетка ТВ: ТВ на стене	2735	1100	
Р4	розетка: ТВ, приставка	3035	1100	рамка 2 поста, гр. 4

Условные обозначения

- розетка с заземляющим контактом; у знака — марка, ×N постов в рамке, гр. — группа щита, Н — высота оси, мм
- ПК — розетка компьютерная RJ45
- ТВ — розетка телевизионная
- привязки точек и выводов от угла и от пола, мм
- A — марка развёртки: буква стены, стрелка — взгляд

Схема развёрток (М 1:200)

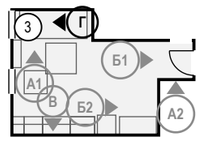


Примечания

1. Вид «Привязки» стены Г — электроточки и выводы ВК; архитектурная развёртка (мебель, отделка, проёмы, высоты) — на листе 51. Мебель и приборы — подложкой для ориентира; их марки и обозначения мебели, проёмов и стен — там же.
2. Привязки — в мм: по горизонтали от левого чистового угла стены до оси изделия, Н — от чистого пола до оси; все точки — в таблице привязок. Красная цепочка — привязки по осям; точки ближе 120 мм одна к другой в цепочку не дробятся — их привязки только в таблице.
3. У знака — марка электроточки (Р — розетка, S — выключатель, Св — светильник, ЭВ — вывод кабеля); условные обозначения и общие указания — лист 3.
4. Выводы кухонной техники — по утверждённому проекту кухни: привязки выводов даются от осей модулей гарнитура.
5. Линии узора (швы плитки, складки штор, рёбра радиаторов) прерываются у знаков и выносок — просвет между линиями не менее 0,7 мм.

					Проект: Квартира 65 м²	М 1:20
	Лист	№ док.	Подпись	Дата		
Дизайнер	Кырлан А.С.			04.11.26	Привязки электроточек, стена Г. Кухня-гостиная (пом. 3)	Стадия: П; Лист: 52; Листов: 83

Развёртка стены А1

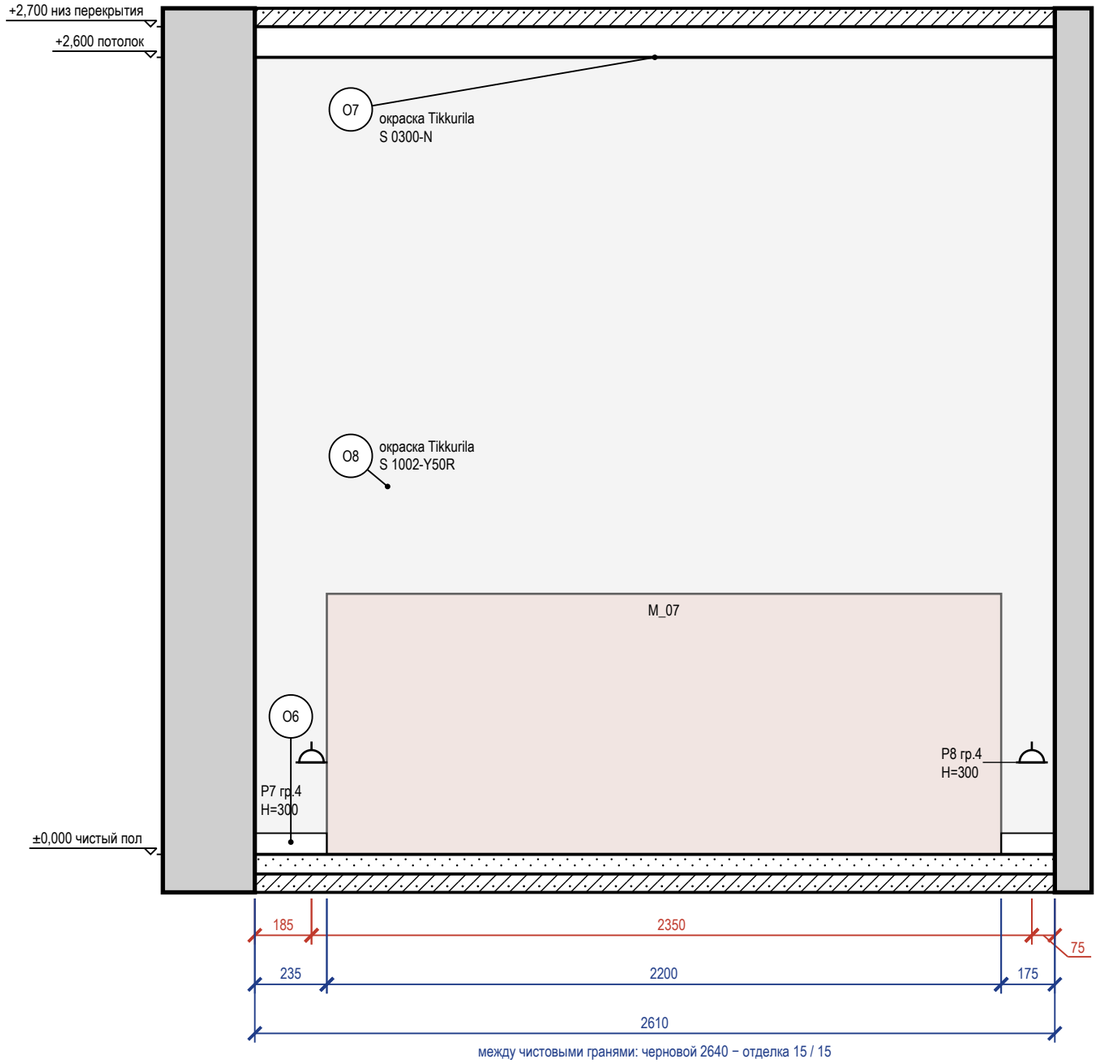

Развёртка стены Б1


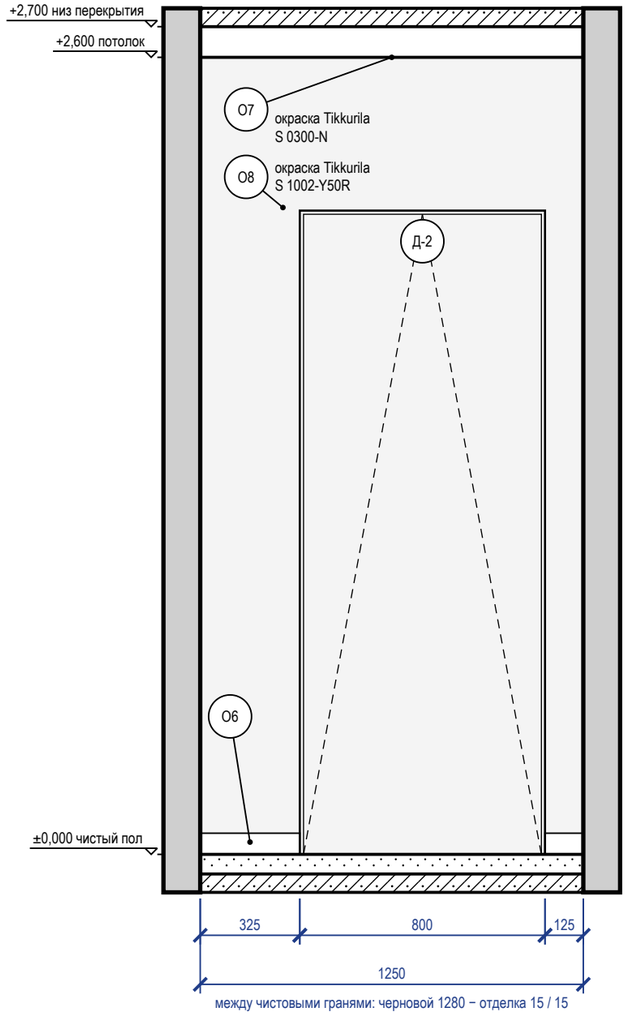


Схема развёрток (М 1:100)

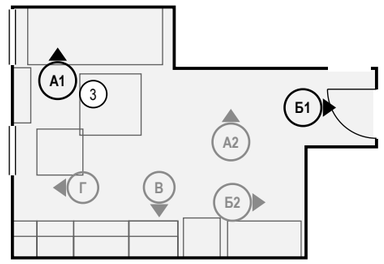

Ведомость отделки (на листе)

Марка	Поверхность	Материал, изделие	Цвет, код	Кол.
О6	плинтус	плинтус МДФ, Orac Decor Contour (Luxxus), h 69 мм, SX165, шелковисто-матовая	NCS S 0300-N	0,9 м
О7	потолок	окраска, Tikkurila, глубокоматовая	NCS S 0300-N	18,9 м²
О8	стены	окраска, Tikkurila, шелковисто-матовая, подготовка Q3	NCS S 1002-Y50R	8,4 м²

Примечания

1. Размеры — в мм от чистовых поверхностей стен; условные обозначения и общие указания — лист 3.
2. Двери скрытого монтажа — полотно в плоскости стены, отделка стены по полотну, плинтус прерывается у короба (узел — на листе узлов).

	Лист	№ док.	Подпись	Дата
Дизайнер	Кырлан А.С.			04.11.26


Проект: Квартира 65 м² — **М 1:20**

Развёртки стен А1, Б1.
Кухня-гостиная (пом. 3)

Стадия	Лист	Листов
П	53	83

выпуск 04.11.2026 № 84932ed378 · стр. 53 из 83

Развёртка стены А2

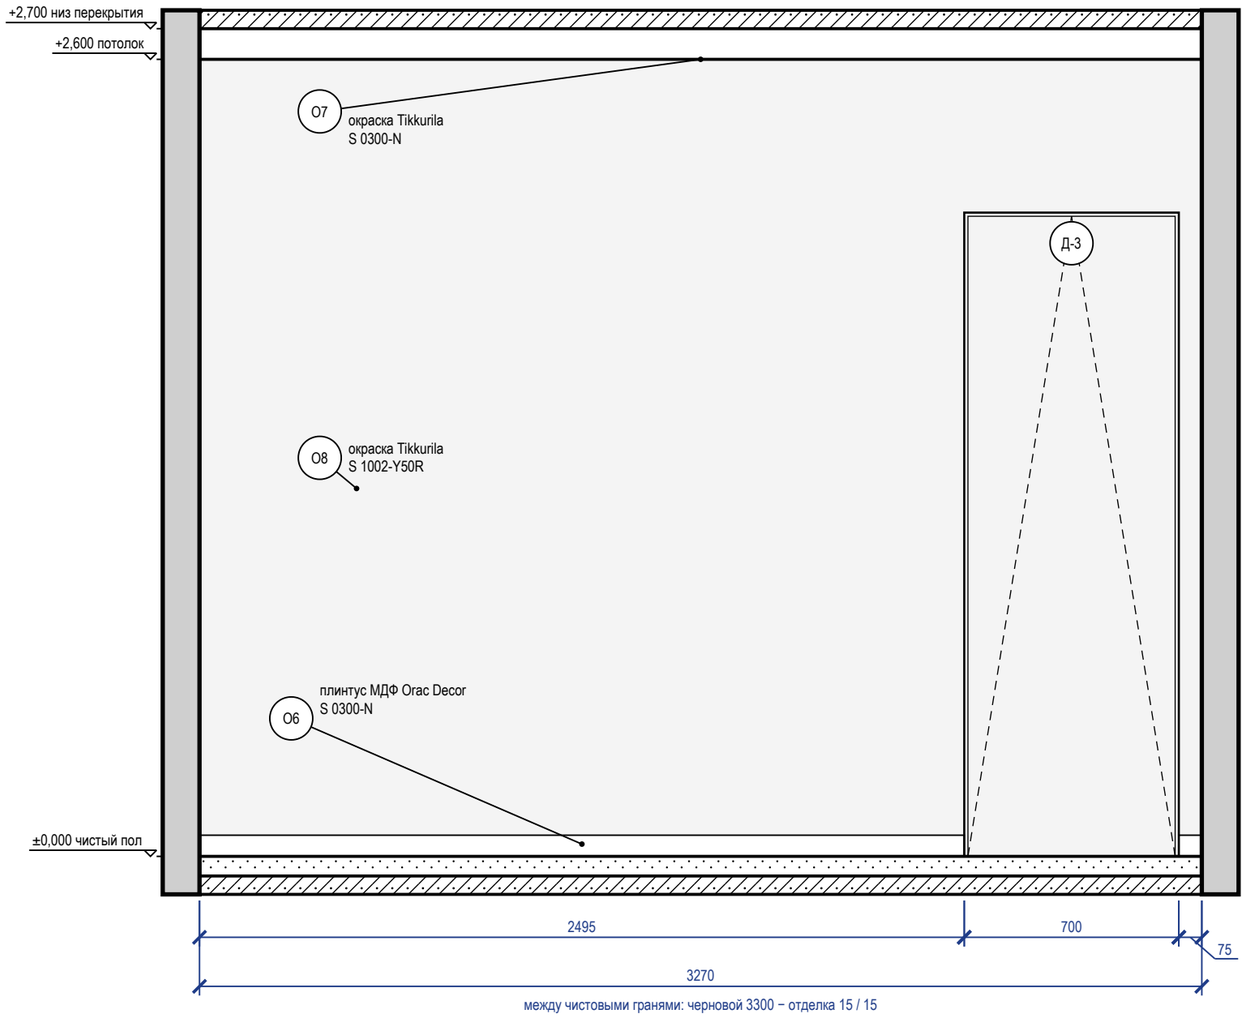

Развёртка стены Б2


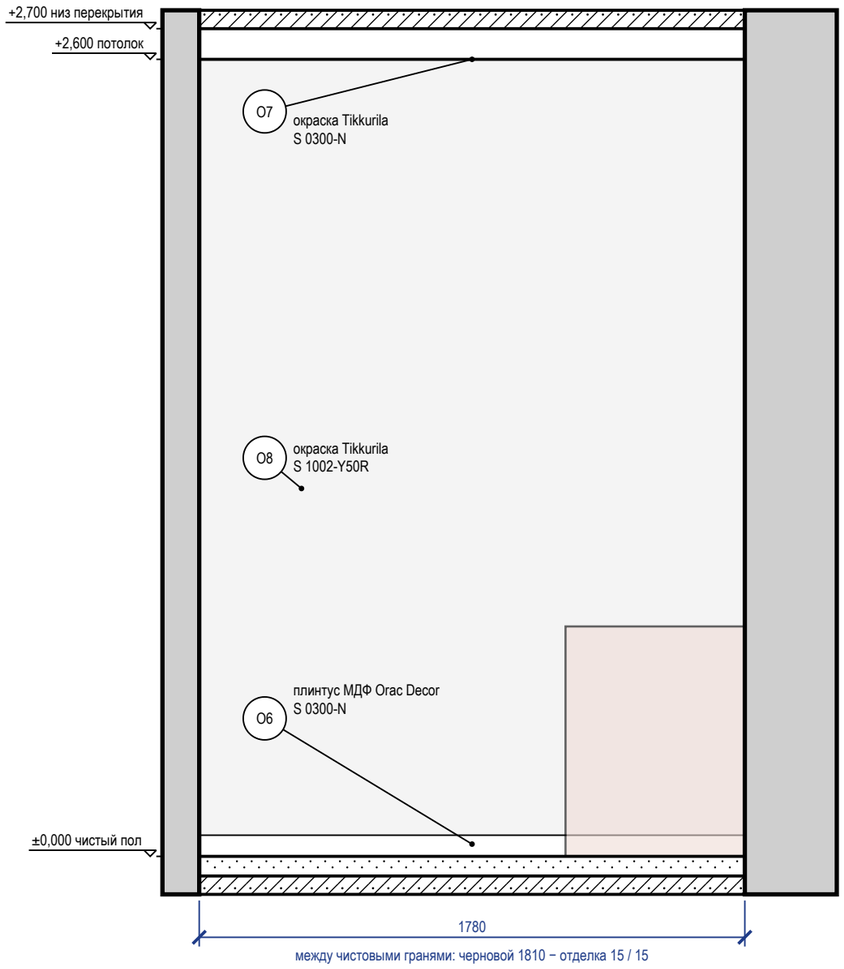


Схема развёрток (М 1:100)

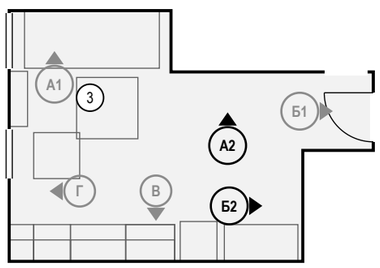

Ведомость отделки (на листе)

Марка	Поверхность	Материал, изделие	Цвет, код	Кол.
О6	плинтус	плинтус МДФ, Orac Decor Contour (Luxxus), h 69 мм, SX165, шелковисто-матовая	NCS S 0300-N	4,3 м
О7	потолок	окраска, Tikkurila, глубокоматовая	NCS S 0300-N	18,9 м²
О8	стены	окраска, Tikkurila, шелковисто-матовая, подготовка Q3	NCS S 1002-Y50R	11,7 м²

Примечания

1. Размеры — в мм от чистовых поверхностей стен; условные обозначения и общие указания — лист 3.
2. Двери скрытого монтажа — полотно в плоскости стены, отделка стены по полотну, плинтус прерывается у короба (узел — на листе узлов).


	Лист	№ док.	Подпись	Дата
Дизайнер	Кырлан А.С.			04.11.26

Проект: Квартира 65 м² — М 1:20

Развёртки стен А2, Б2.
Кухня-гостиная (пом. 3)


Стадия	Лист	Листов
П	54	83

Развёртка стены Б

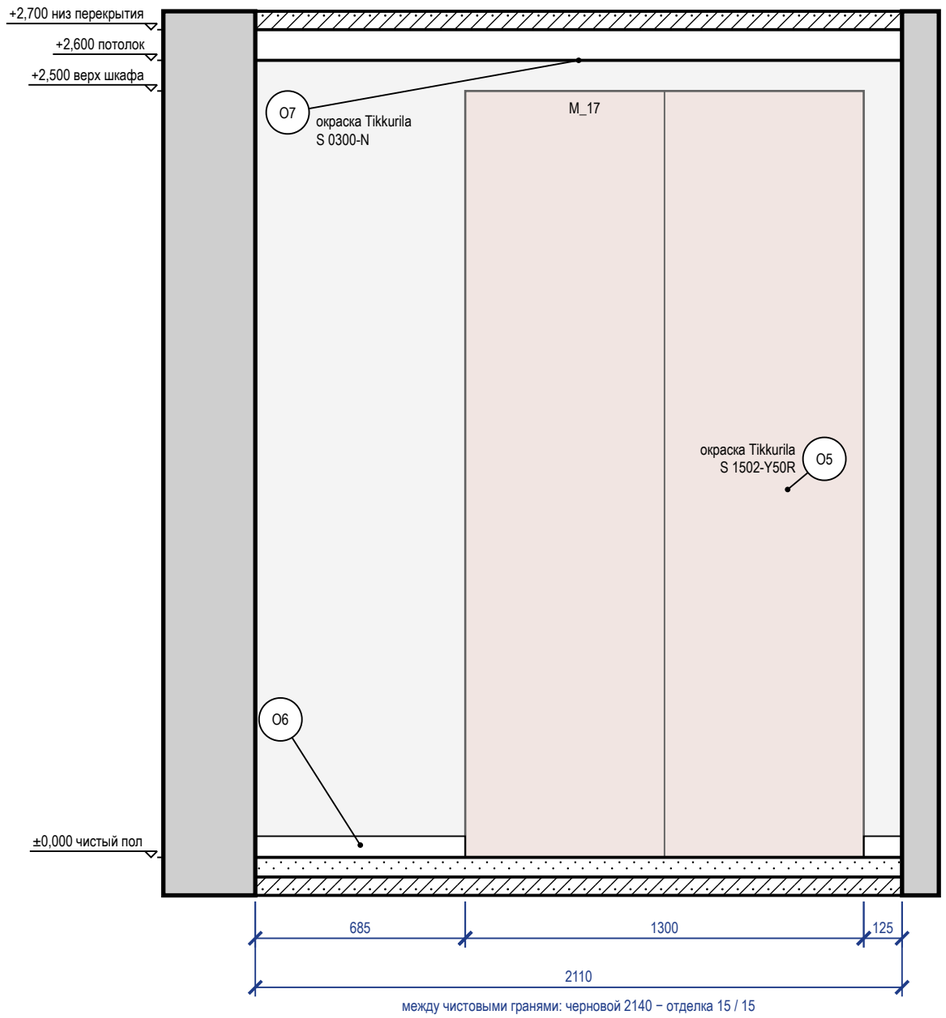


между чистовыми гранями: черновой 2140 − отделка 15 / 15

Развёртка стены Г

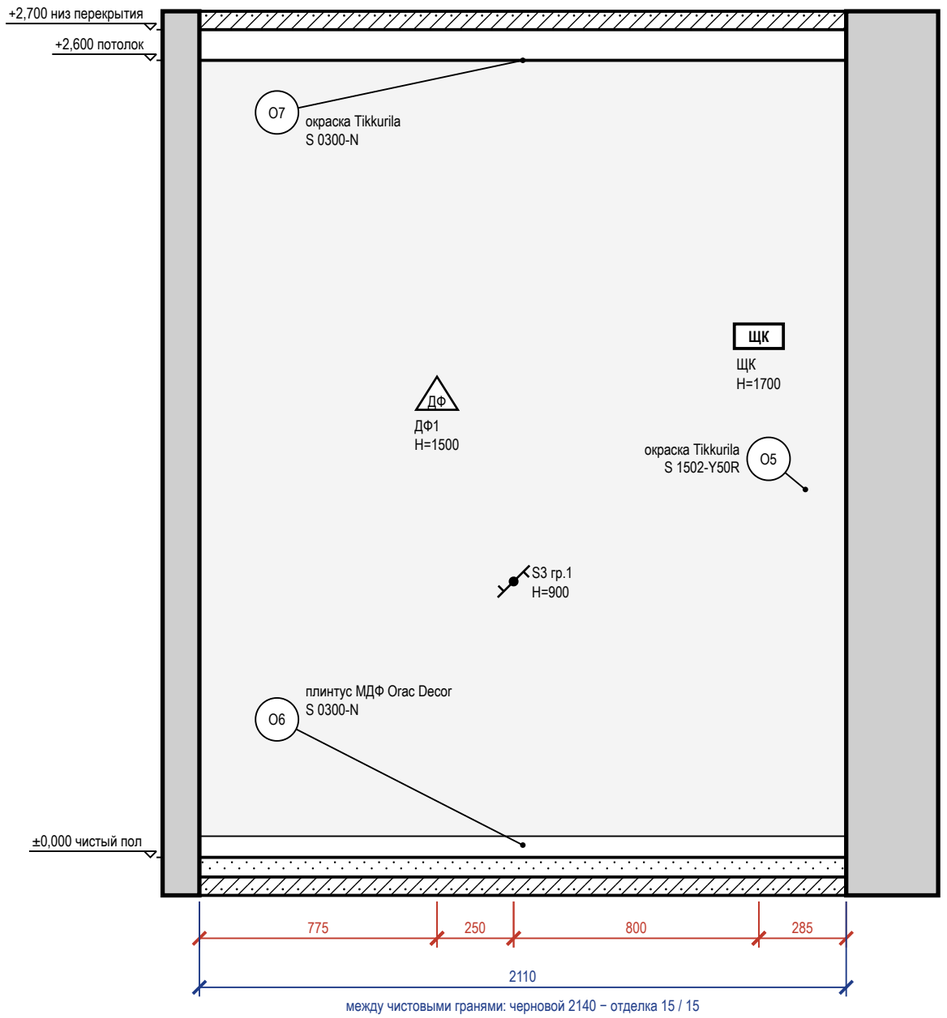

между чистовыми гранями: черновой 2140 − отделка 15 / 15

Схема развёрток (М 1:100)

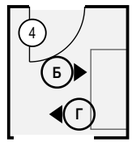

Ведомость отделки (на листе)


Марка	Поверхность	Материал, изделие	Цвет, код	Кол.
О5	стены	окраска, Tikkurila, шелковисто-матовая, подготовка Q3	NCS S 1502-Y50R	11 м²
О6	плинтус	плинтус МДФ, Orac Decor Contour (Luxxus), h 69 мм, SX165, шелковисто-матовая	NCS S 0300-N	2,9 м
О7	потолок	окраска, Tikkurila, глубокоматовая	NCS S 0300-N	4,2 м²

Примечания

1. Размеры — в мм от чистовых поверхностей стен; условные обозначения и общие указания — лист 3.


					Проект: Квартира 65 м²	М 1:20
	Лист	№ док.	Подпись	Дата	Развёртки стен. Прихожая (пом. 4)	Стадия / Лист / Листов
Дизайнер	Кырлан А.С.			04.11.26		П / 55 / 83

Развёртка стены А

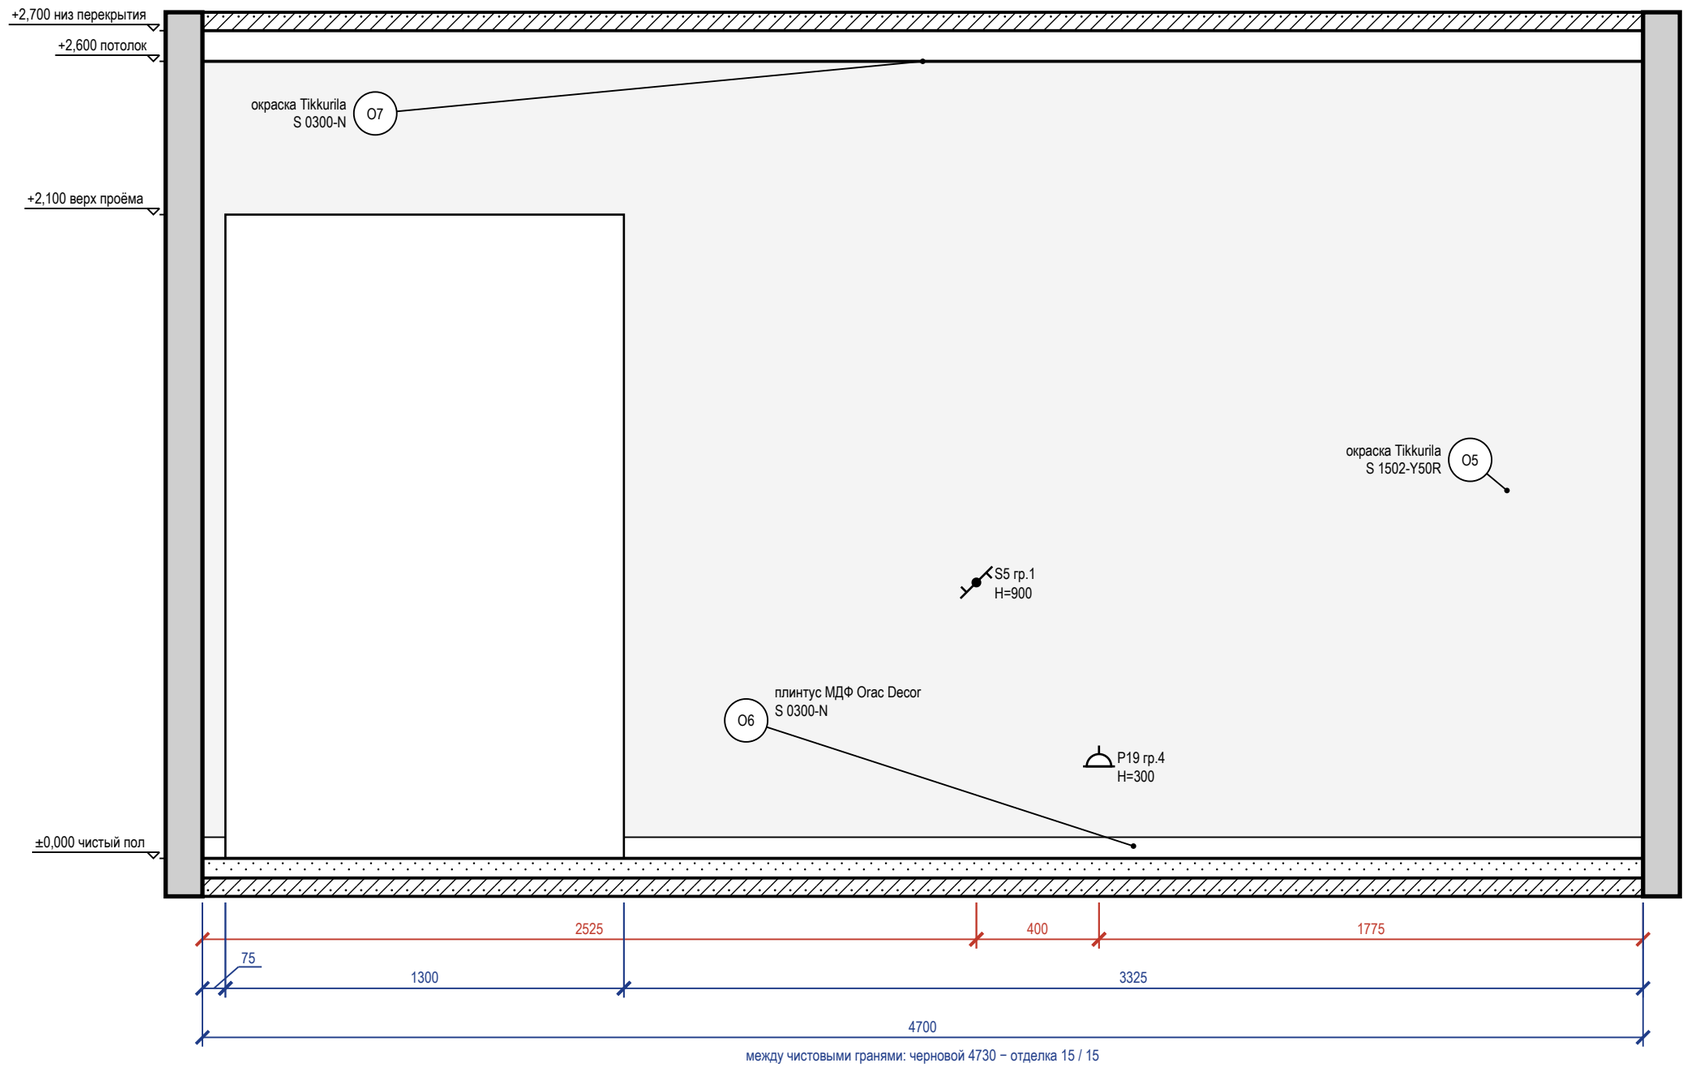

между чистовыми гранями: черновой 4730 − отделка 15 / 15

Схема развёрток (М 1:100)

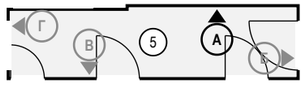

Ведомость отделки (на листе)


Марка	Поверхность	Материал, изделие	Цвет, код	Кол.
O5	стены	окраска, Tikkurila, шелковисто-матовая, подготовка Q3	NCS S 1502-Y50R	9,5 м²
O6	плинтус	плинтус МДФ, Orac Decor Contour (Luxxus), h 69 мм, SX165, шелковисто-матовая	NCS S 0300-N	3,4 м
O7	потолок	окраска, Tikkurila, глубокоматовая	NCS S 0300-N	5,5 м²

Примечания

1. Размеры — в мм от чистовых поверхностей стен; условные обозначения и общие указания — лист 3.

					Проект: Квартира 65 м² — М 1:20
	Лист	№ док.	Подпись	Дата	Развёртка стены А. Коридор (пом. 5)
Дизайнер	Кырлан А.С.			04.11.26	Стадия: П · Лист: 56 · Листов: 83

Развёртка стены Б

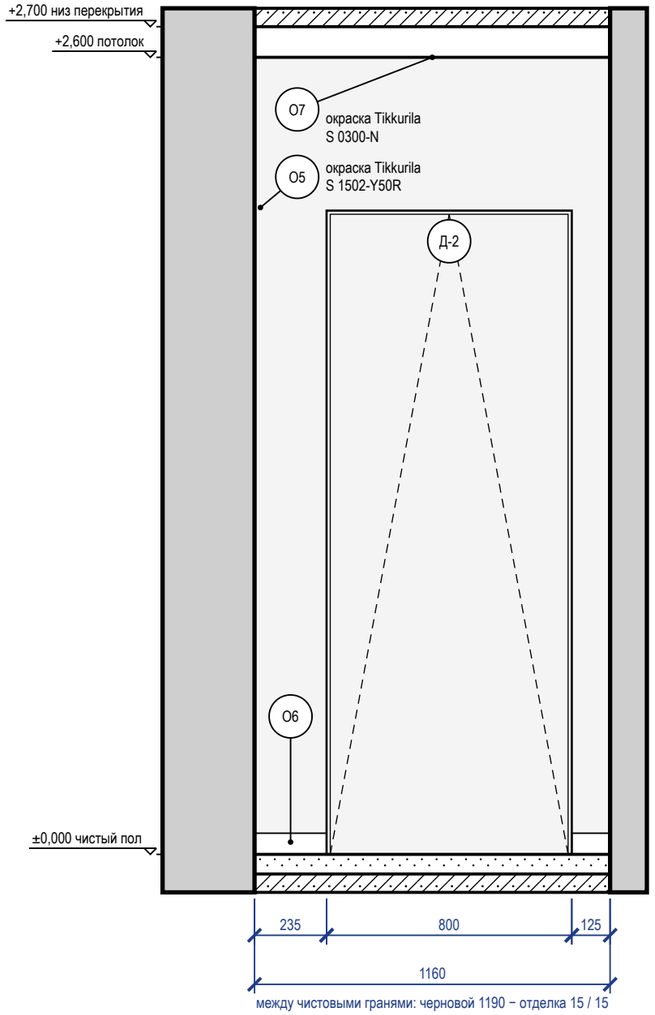

Развёртка стены Г


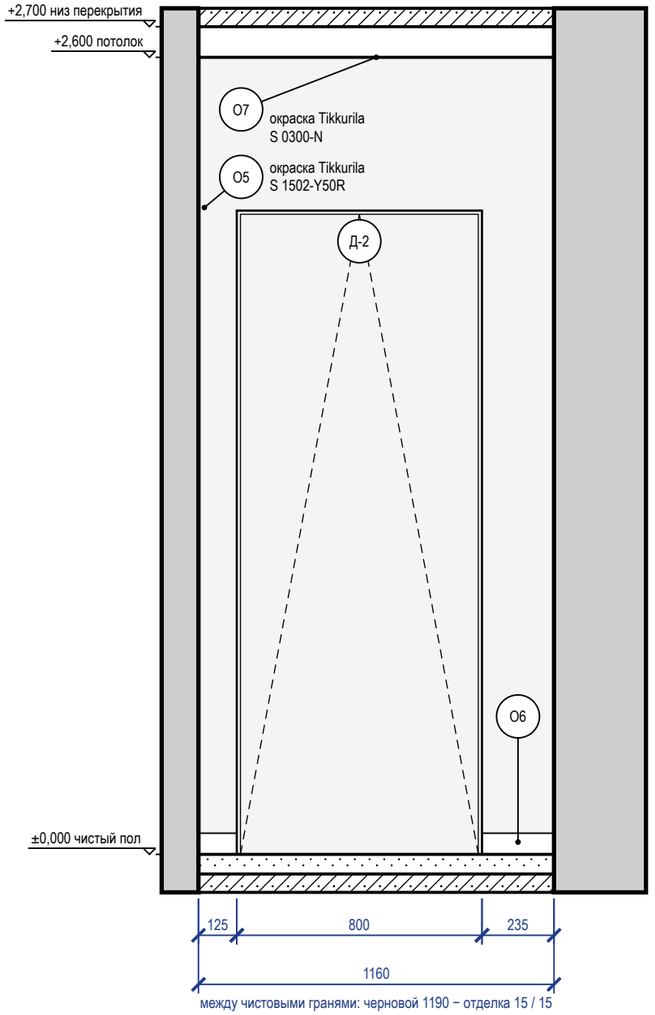


Схема развёрток (М 1:100)

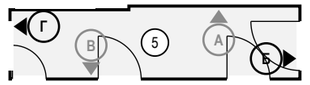

Ведомость отделки (на листе)

Марка	Поверхность	Материал, изделие	Цвет, код	Кол.
О5	стены	окраска, Tikkurila, шелковисто-матовая, подготовка Q3	NCS S 1502-Y50R	2,7 м²
О6	плинтус	плинтус МДФ, Orac Decor Contour (Luxxus), h 69 мм, SX165, шелковисто-матовая	NCS S 0300-N	0,7 м
О7	потолок	окраска, Tikkurila, глубокоматовая	NCS S 0300-N	5,5 м²

Примечания

1. Размеры — в мм от чистовых поверхностей стен; условные обозначения и общие указания — лист 3.
2. Двери скрытого монтажа — полотно в плоскости стены, отделка стены по полотну, плинтус прерывается у короба (узел — на листе узлов).

					Проект: Квартира 65 м²	М 1:20
	Лист	№ док.	Подпись	Дата	Развёртки стен Б, Г. Коридор (пом. 5)	Стадия / Лист / Листов
Дизайнер	Кырлан А.С.			04.11.26		П / 57 / 83

Развёртка стены В


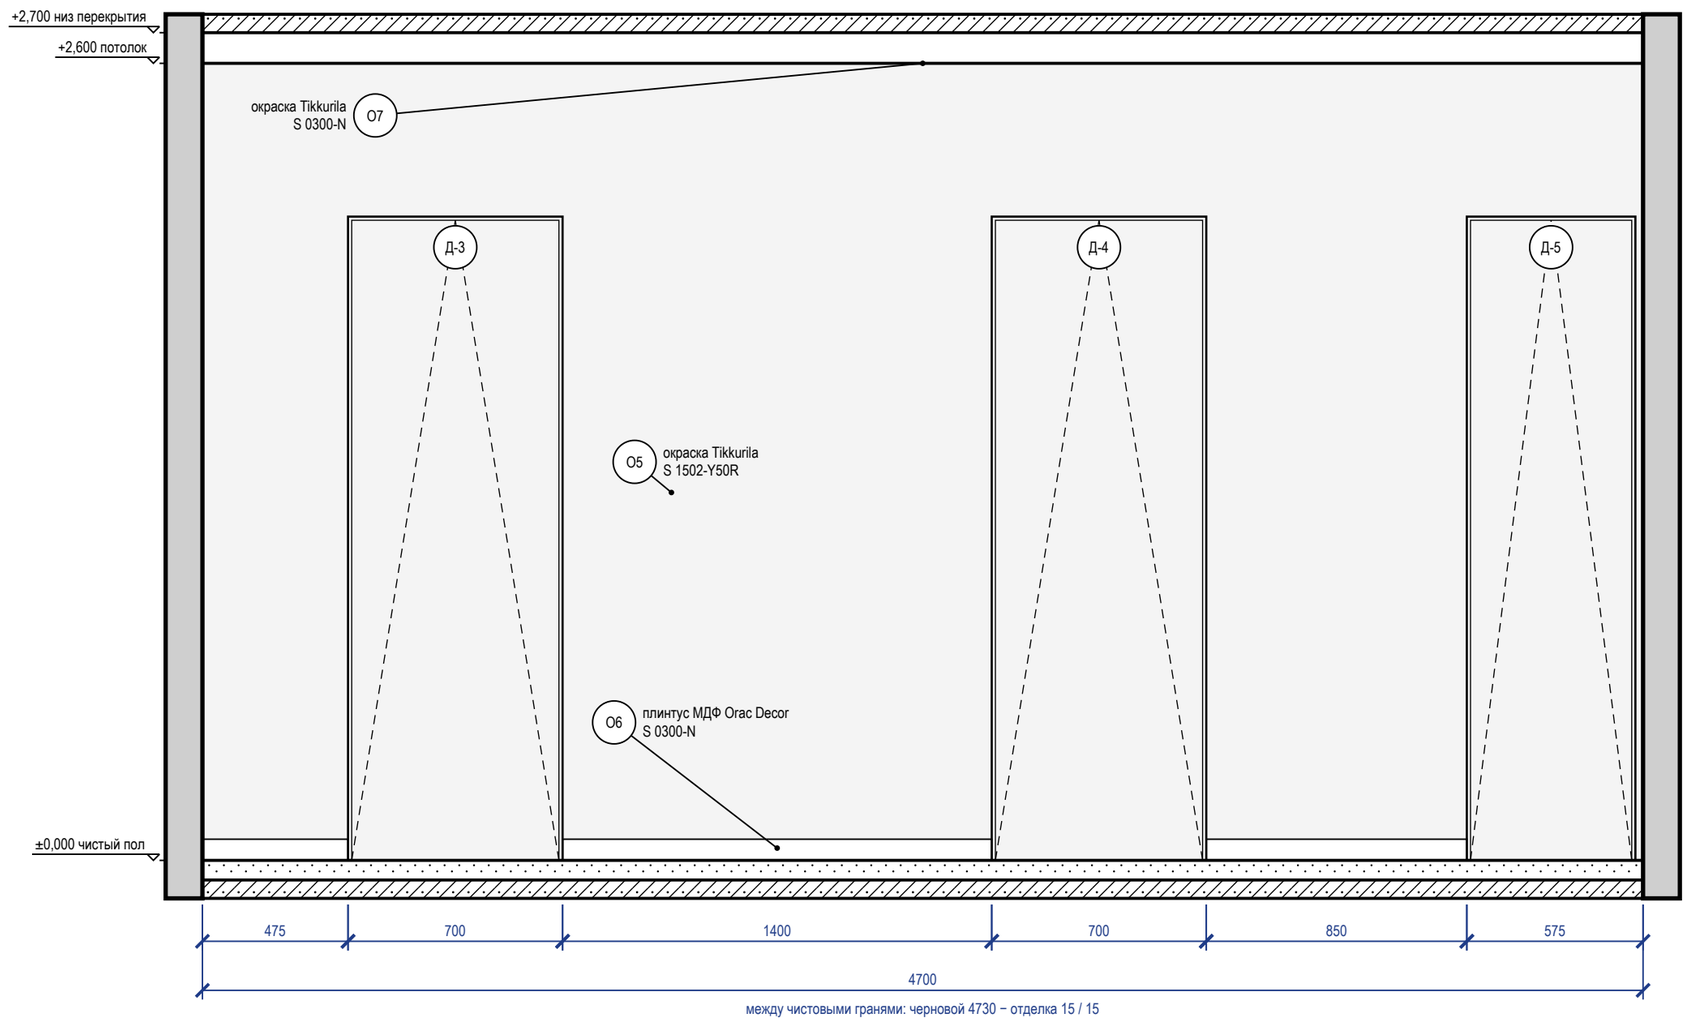


Схема развёрток (М 1:100)

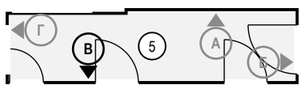

Ведомость отделки (на листе)

Марка	Поверхность	Материал, изделие	Цвет, код	Кол.
О5	стены	окраска, Tikkurila, шелковисто-матовая, подготовка Q3	NCS S 1502-Y50R	8,1 м²
О6	плинтус	плинтус МДФ, Orac Decor Contour (Luxxus), h 69 мм, SX165, шелковисто-матовая	NCS S 0300-N	2,7 м
О7	потолок	окраска, Tikkurila, глубокоматовая	NCS S 0300-N	5,5 м²


Примечания

1. Размеры — в мм от чистовых поверхностей стен; условные обозначения и общие указания — лист 3.
2. Двери скрытого монтажа — полотно в плоскости стены, отделка стены по полотну, плинтус прерывается у короба (узел — на листе узлов).

					Проект: Квартира 65 м²	М 1:20
	Лист	№ док.	Подпись	Дата	Развёртка стены В. Коридор (пом. 5)	Стадия / Лист / Листов
Дизайнер	Кырлан А.С.			04.11.26		П / 58 / 83


выпуск 04.11.2026 № 84932ed378 · стр. 58 из 83

Развёртка стены А

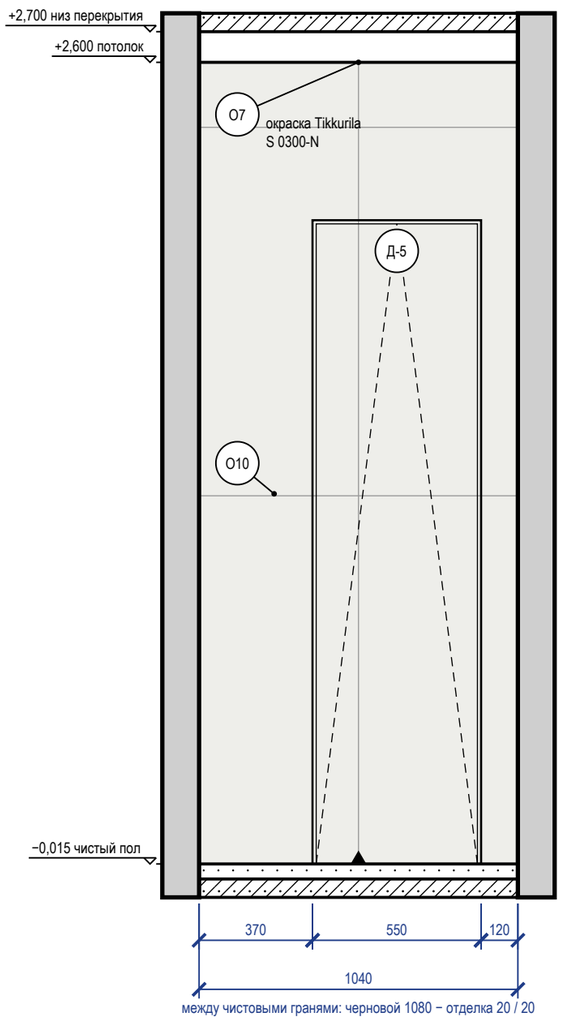


между чистовыми гранями: черновой 1080 − отделка 20 / 20

Развёртка стены Б

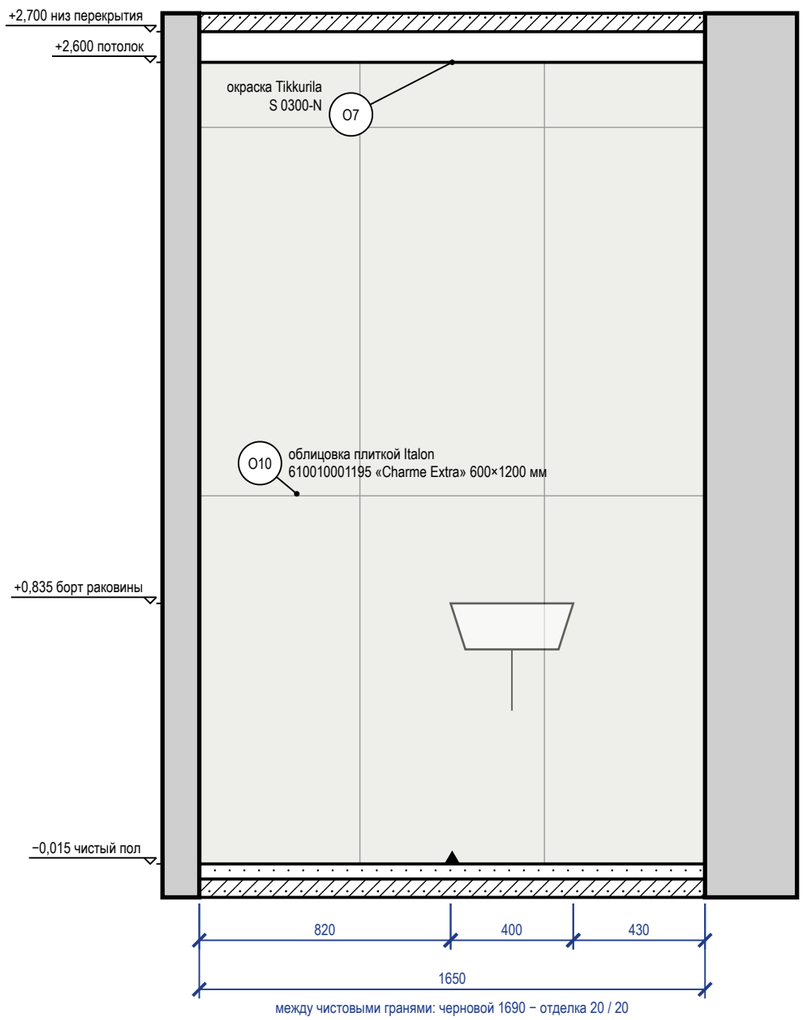


между чистовыми гранями: черновой 1690 − отделка 20 / 20

Развёртка стены В

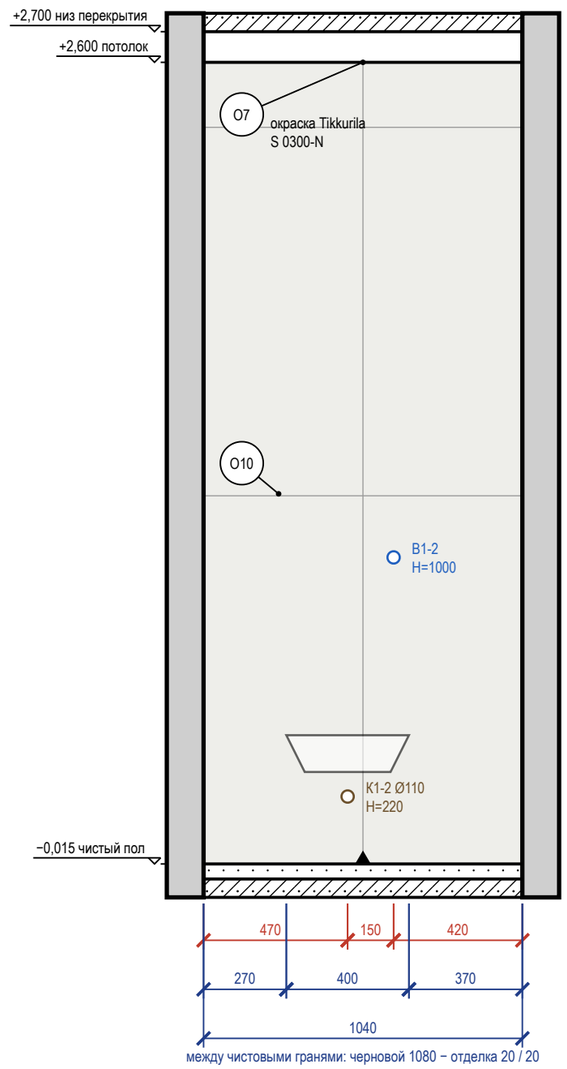

между чистовыми гранями: черновой 1080 − отделка 20 / 20

Схема развёрток (М 1:100)

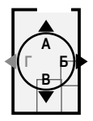

Ведомость отделки (на листе)

Марка	Поверхность	Материал, изделие	Цвет, код	Кол.
О7	потолок	окраска, Tikkurila, глубокоматовая	NCS S 0300-N	1,8 м²
О10	стены	облицовка плиткой, Italon Charme Extra, 600×1200 мм, 610010001195	Italon 610010001195 «Charme Extra»	8,6 м²

Примечания

1. Размеры — в мм от чистовых поверхностей стен; условные обозначения и общие указания — лист 3.
2. Стена Б показана двумя видами: здесь — архитектурная развёртка (мебель, отделка, проёмы, высоты), электроточки и выводы ВК с привязками и таблицей — на листе 60 («Привязки»).
3. Схема мебели, приборов и декора не является технической документацией для производства мебели; габариты — по паспортам изделий.
4. Облицовка — по сетке швов, раскладка от оси стены (треугольник у пола); подрезки — по листу раскладки плитки.
5. Гидроизоляция в 2 слоя, заход на стены 200 мм — до облицовки, с актом скрытых работ и тестом проливом (узел — на листе узлов).
6. Двери скрытого монтажа — полотно в плоскости стены, отделка стены по полотну, плинтус прерывается у короба (узел — на листе узлов).

					Проект: Квартира 65 м² — М 1:20
	Лист	№ док.	Подпись	Дата	Развёртки стен А, Б, В. Санузел (пом. 6)
Дизайнер	Кырлан А.С.			04.11.26	Стадия: П; Лист: 59; Листов: 83

Развёртка стены Б: электроточки и выводы

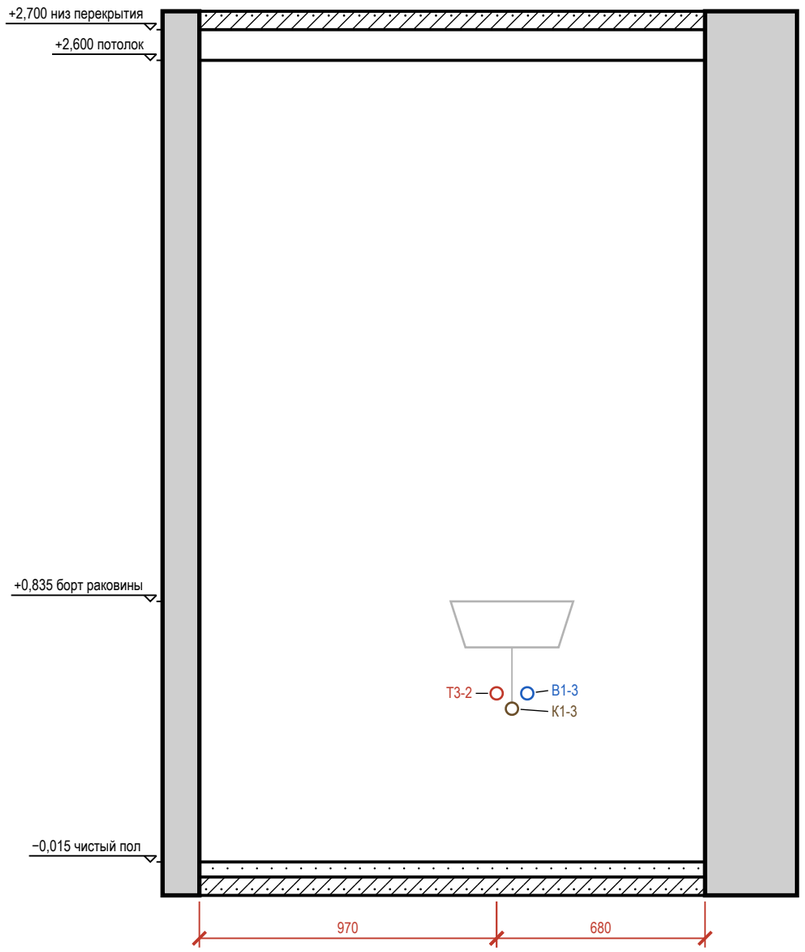



Таблица привязок электроточек и выводов

Марка	Назначение	От угла, мм	Н от пола, мм	Примечание
Т3-2	горячая вода — умывальник	970	550	межос. 100
К1-3	канализация — умывальник	1020	500	Ø50
В1-3	холодная вода — умывальник	1070	550	межос. 100

Условные обозначения

- вывод В1 (код — в ведомости привязок)
- вывод Т3 (код — в ведомости привязок)
- вывод К1 (код — в ведомости привязок)
- привязки точек и выводов от угла и от пола, мм
- марка развёртки: буква стены, стрелка — взгляд

Схема развёрток (М 1:50)

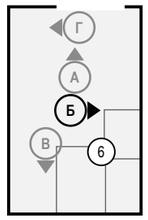

Примечания

1. Вид «Привязки» стены Б — электроточки и выводы ВК; архитектурная развёртка (мебель, отделка, проёмы, высоты) — на листе 59. Мебель и приборы — подложкой для ориентира; их марки и обозначения мебели, проёмов и стен — там же.
2. Привязки — в мм: по горизонтали от левого чистового угла стены до оси изделия, Н — от чистого пола до оси; все точки — в таблице привязок. Красная цепочка — привязки по осям; точки ближе 120 мм одна к другой в цепочку не дробятся — их привязки только в таблице.
3. Коды выводов ВК: В1 — холодная вода, Т3 — горячая вода, К1 — канализация; номер после дефиса — номер вывода на листе выводов сантехники.

					Проект: Квартира 65 м²	М 1:20
	Лист	№ док.	Подпись	Дата		
Дизайнер	Кырлан А.С.			04.11.26	Привязки выводов ВК, стена Б. Санузел (пом. 6)	Стадия: П; Лист: 60; Листов: 83

Развёртка стены Г


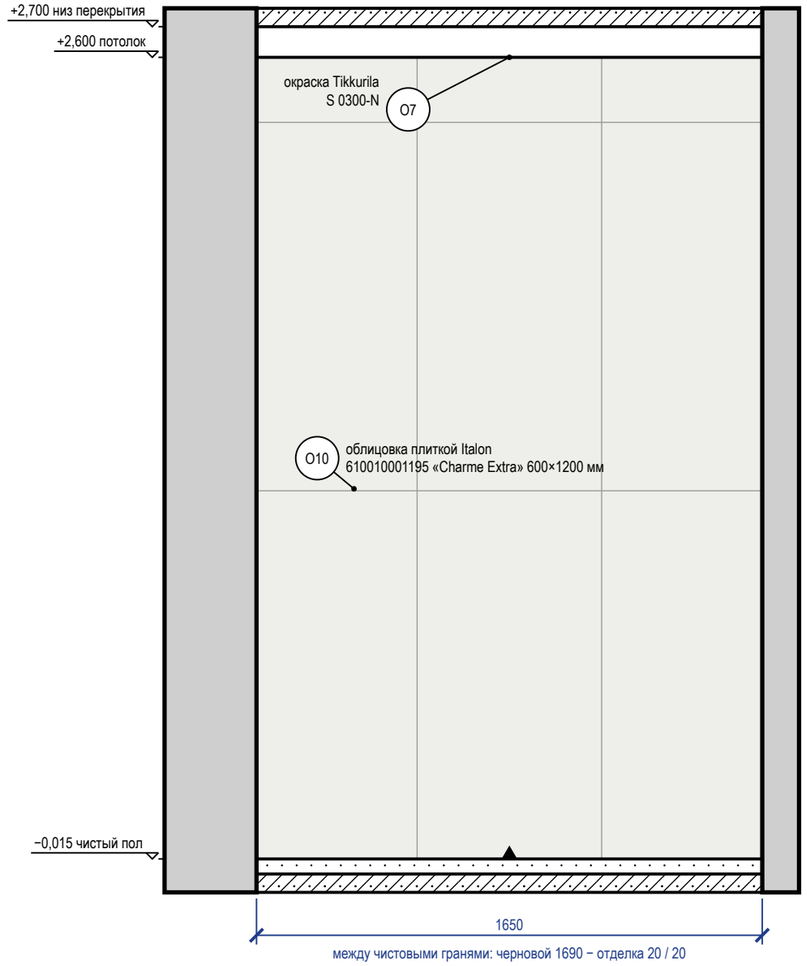


Схема развёрток (М 1:100)

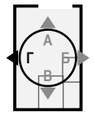


Ведомость отделки (на листе)

Марка	Поверхность	Материал, изделие	Цвет, код	Кол.
О7	потолок	окраска, Tikkurila, глубокоматовая	NCS S 0300-N	1,8 м²
О10	стены	облицовка плиткой, Italon Charme Extra, 600×1200 мм, 610010001195	Italon 610010001195 «Charme Extra»	4,3 м²

3 **Короб стояков К1-1 с люком и звукоизоляцией (М 1:20)**

Узел 3 — лист С6

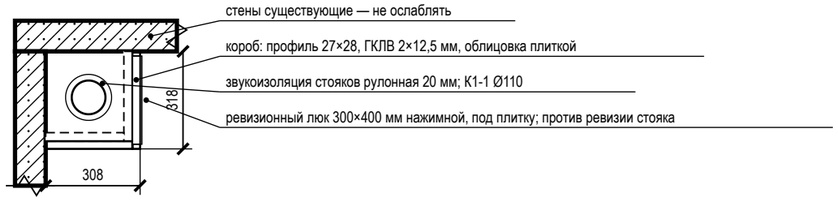


Примечания

1. Размеры — в мм от чистовых поверхностей стен; условные обозначения и общие указания — лист 3.
2. Облицовка — по сетке швов, раскладка от оси стены (треугольник у пола); подрезки — по листу раскладки плитки.
3. Гидроизоляция в 2 слоя, заход на стены 200 мм — до облицовки, с актом скрытых работ и тестом проливом (узел — на листе узлов).


					Проект: Квартира 65 м²	М 1:20
	Лист	№ док.	Подпись	Дата		
Дизайнер	Кырлан А.С.			04.11.26	Развёртка стены Г. Санузел (пом. 6)	Стадия: П; Лист: 61; Листов: 83

Развёртка стены А

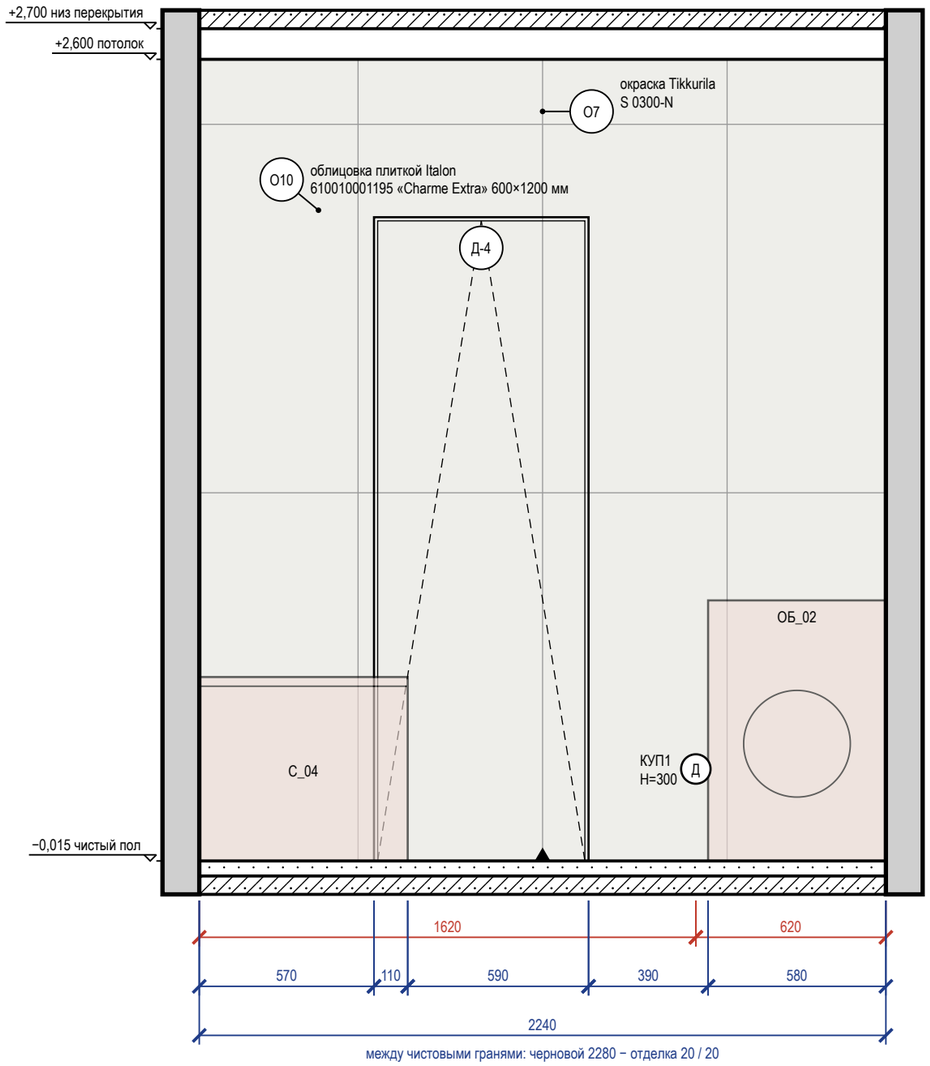


между чистовыми гранями: черновой 2280 − отделка 20 / 20

Развёртка стены Б

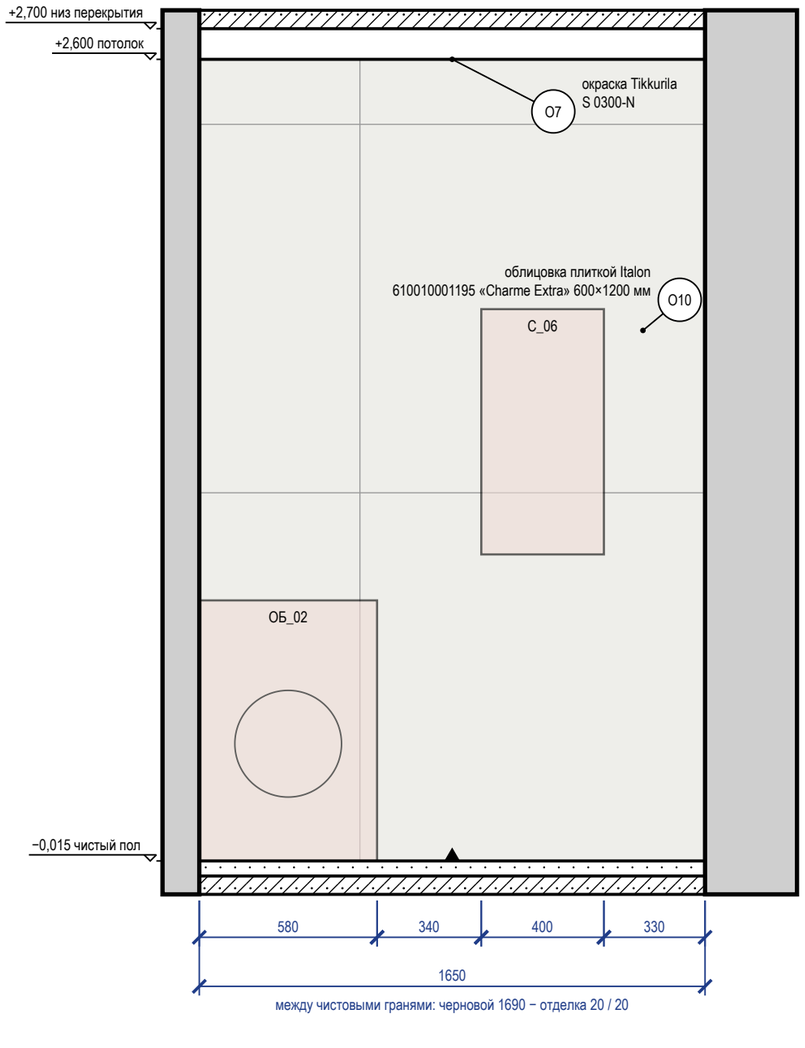

между чистовыми гранями: черновой 1690 − отделка 20 / 20

Схема развёрток (М 1:100)

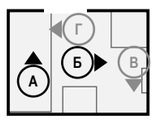

Ведомость отделки (на листе)


Марка	Поверхность	Материал, изделие	Цвет, код	Кол.
О7	потолок	окраска, Tikkurila, глубокоматовая	NCS S 0300-N	3,9 м²
О10	стены	облицовка плиткой, Italon Charme Extra, 600×1200 мм, 610010001195	Italon 610010001195 «Charme Extra»	8,7 м²

Примечания

1. Размеры — в мм от чистовых поверхностей стен; условные обозначения и общие указания — лист 3.
2. Стена Б показана двумя видами: здесь — архитектурная развёртка (мебель, отделка, проёмы, высоты), электроточки и выводы ВК с привязками и таблицей — на листе 64 («Привязки»).
3. Схема мебели, приборов и декора не является технической документацией для производства мебели; габариты — по паспортам изделий.
4. Облицовка — по сетке швов, раскладка от оси стены (треугольник у пола); подрезки — по листу раскладки плитки.
5. Гидроизоляция в 2 слоя, заход на стены 200 мм; над ванной — до 2000 и 300 мм за борт — до облицовки, с актом скрытых работ и тестом проливом (узел — на листе узлов).
6. Двери скрытого монтажа — полотно в плоскости стены, отделка стены по полотну, плинтус прерывается у короба (узел — на листе узлов).


					Проект: Квартира 65 м²	М 1:20
	Лист	№ док.	Подпись	Дата		
Дизайнер	Кырлан А.С.			04.11.26	Развёртки стен А, Б. Ванная (пом. 7)	
					Стадия: П	Лист: 62 / Листов: 83

Развёртка стены В

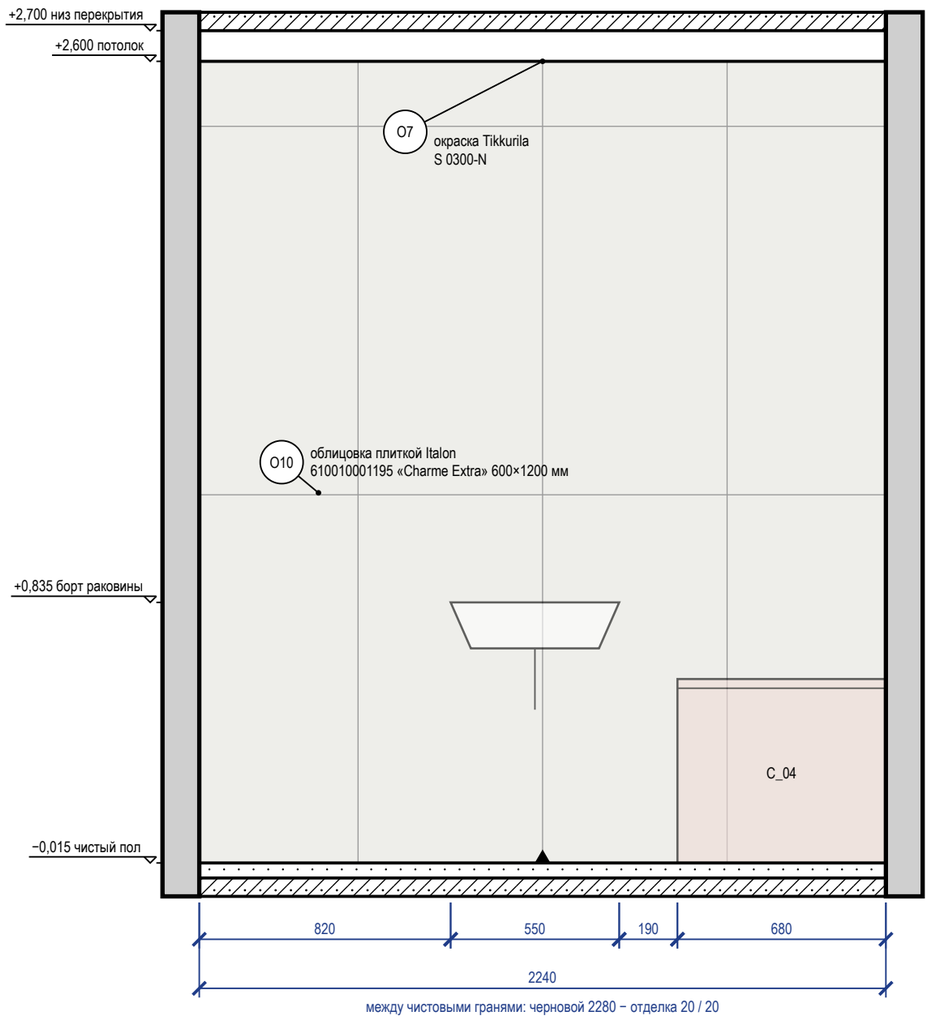


между чистовыми гранями: черновой 2280 − отделка 20 / 20

Развёртка стены Г

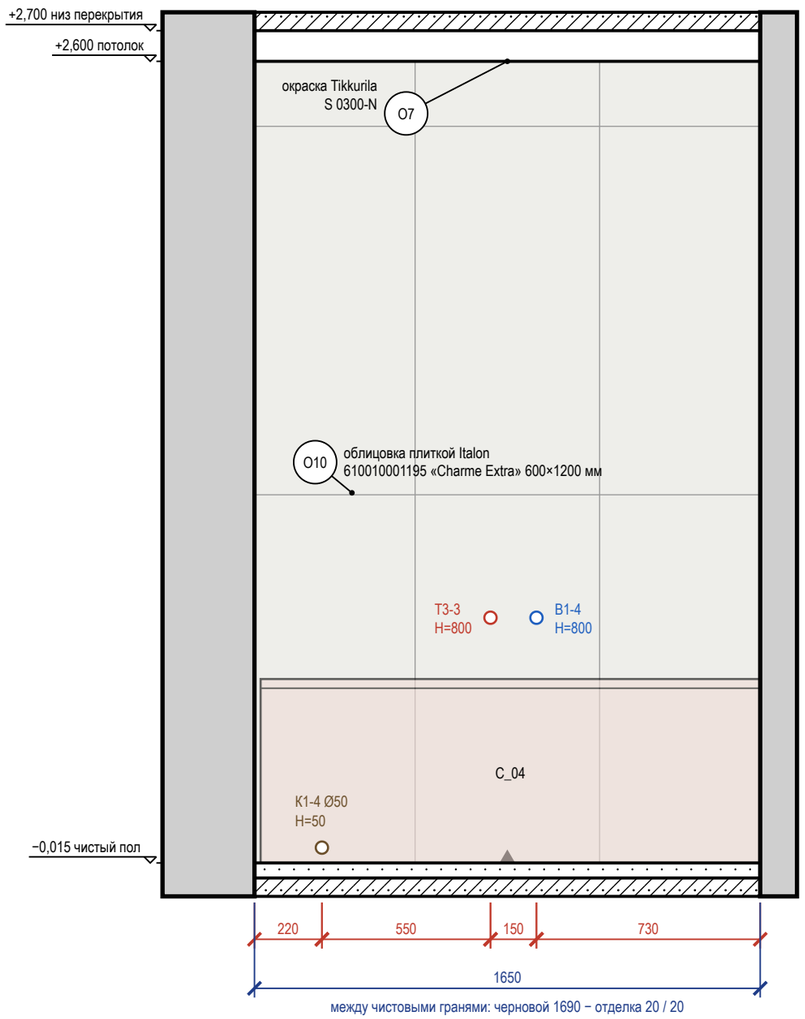

между чистовыми гранями: черновой 1690 − отделка 20 / 20

Схема развёрток (М 1:100)

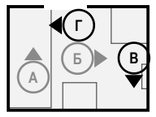

Ведомость отделки (на листе)


Марка	Поверхность	Материал, изделие	Цвет, код	Кол.
О7	потолок	окраска, Tikkurila, глубокоматовая	NCS S 0300-N	3,9 м²
О10	стены	облицовка плиткой, Italon Charme Extra, 600×1200 мм, 610010001195	Italon 610010001195 «Charme Extra»	10,2 м²

Примечания

1. Размеры — в мм от чистовых поверхностей стен; условные обозначения и общие указания — лист 3.
2. Стена В показана двумя видами: здесь — архитектурная развёртка (мебель, отделка, проёмы, высоты), электроточки и выводы ВК с привязками и таблицей — на листе 64 («Привязки»).
3. Облицовка — по сетке швов, раскладка от оси стены (треугольник у пола); подрезки — по листу раскладки плитки.
4. Гидроизоляция в 2 слоя, заход на стены 200 мм; над ванной — до 2000 и 300 мм за борт — до облицовки, с актом скрытых работ и тестом проливом (узел — на листе узлов).

					Проект: Квартира 65 м²	М 1:20
	Лист	№ док.	Подпись	Дата	Развёртки стен В, Г. Ванная (пом. 7)	Стадия / Лист / Листов
Дизайнер	Кырлан А.С.			04.11.26		П / 63 / 83

Развёртка стены Б: электроточки и выводы

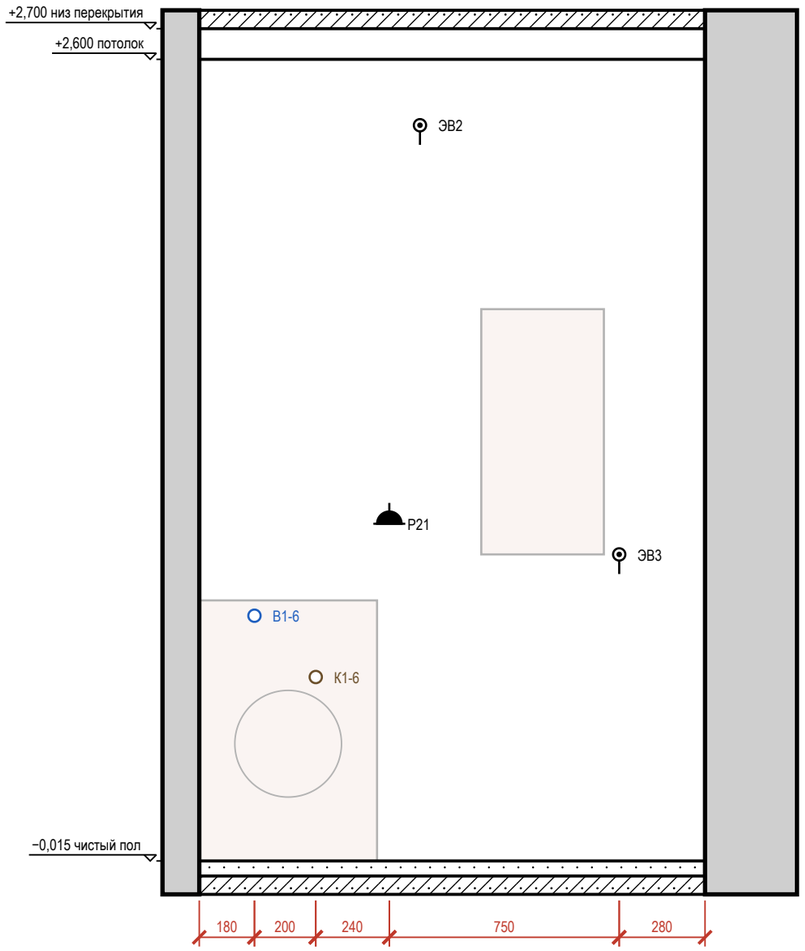

Развёртка стены В: электроточки и выводы

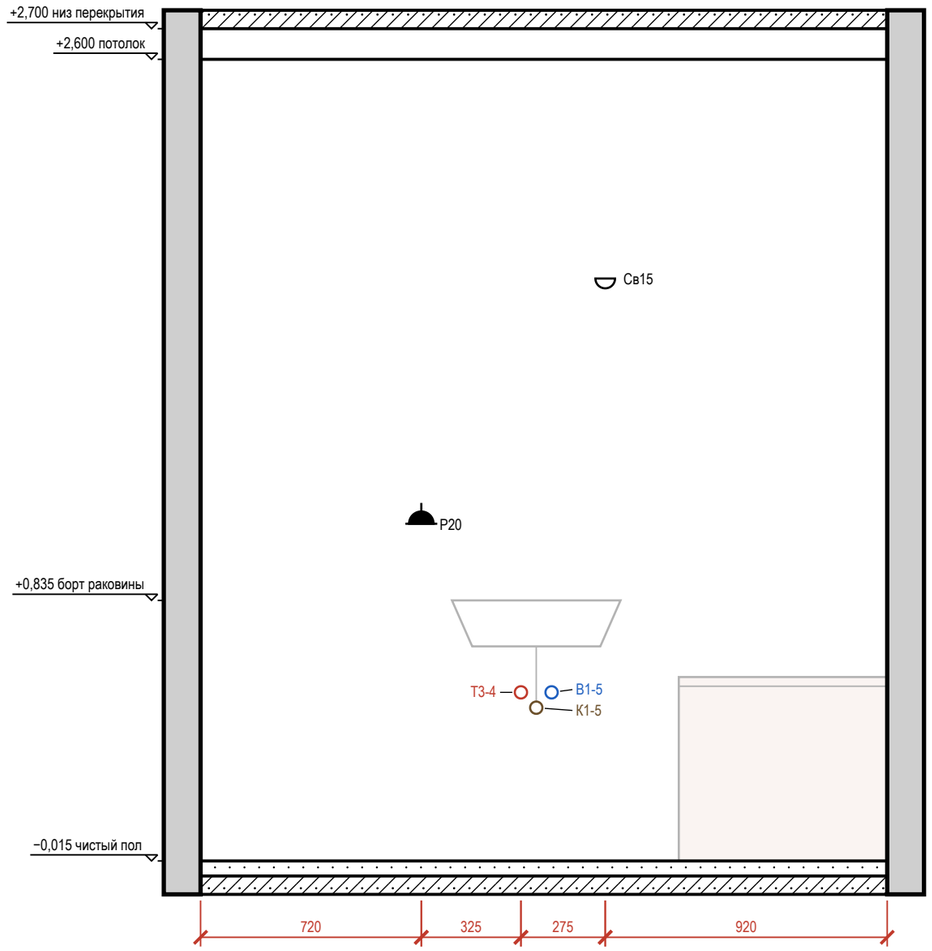


Таблица привязок электроточек и выводов

Стена	Марка	Назначение	От угла, мм	Н от пола, мм	Примечание
Б	В1-6	холодная вода — стиральная машина	180	800	кран машины
Б	К1-6	канализация — стиральная машина	380	600	Ø50
Б	Р21	розетка: стиральная машина	620	1100	гр. 5, IP44
Б	ЭВ2	вывод кабеля: вентилятор (клавиша L4, таймер выбега)	720	2400	гр. 1
Б	ЭВ3	вывод кабеля: полотенцесушитель	1370	1000	гр. 5

Стена	Марка	Назначение	От угла, мм	Н от пола, мм	Примечание
В	Р20	розетка: фен	720	1100	гр. 5, IP44
В	Т3-4	горячая вода — умывальник	1045	550	межос. 100
В	К1-5	канализация — умывальник	1095	500	Ø50
В	В1-5	холодная вода — умывальник	1145	550	межос. 100
В	Св15	светильник настенный	1320	1900	гр. 1

Условные обозначения

- розетка влагозащищённая IP44
- вывод кабеля для подключения прибора (без розетки), марка ЭВ
- светильник настенный (бра), Н — высота оси
- вывод В1 (код — в ведомости привязок)
- вывод Т3 (код — в ведомости привязок)
- вывод К1 (код — в ведомости привязок)
- привязки точек и выводов от угла и от пола, мм


Примечания

1. Вид «Привязки» стен Б, В — электроточки и выводы ВК; архитектурная развёртка (мебель, отделка, проёмы, высоты) — на листах 62, 63. Мебель и приборы подложкой для ориентира; их марки и обозначения мебели, проёмов и стен — там же.
2. Привязки — в мм: по горизонтали от левого чистового угла стены до оси изделия, Н — от чистого пола до оси; все точки — в таблице привязок. Красная цепочка — привязки по осям; точки ближе 120 мм одна к другой в цепочку не дробятся — их привязки только в таблице.
3. У знака — марка электроточки (Р — розетка, S — выключатель, Св — светильник, ЭВ — вывод кабеля); условные обозначения и общие указания — лист 3.
4. Коды выводов ВК: В1 — холодная вода, Т3 — горячая вода, К1 — канализация; номер после дефиса — номер вывода на листе выводов сантехники.

					Проект: Квартира 65 м² — М 1:20
	Лист	№ док.	Подпись	Дата	Привязки электроточек и выводов ВК, стены Б, В. Ванная (пом. 7)
Дизайнер	Кырлан А.С.			04.11.26	


Стадия	Лист	Листов
П	64	83

Развёртка стены А

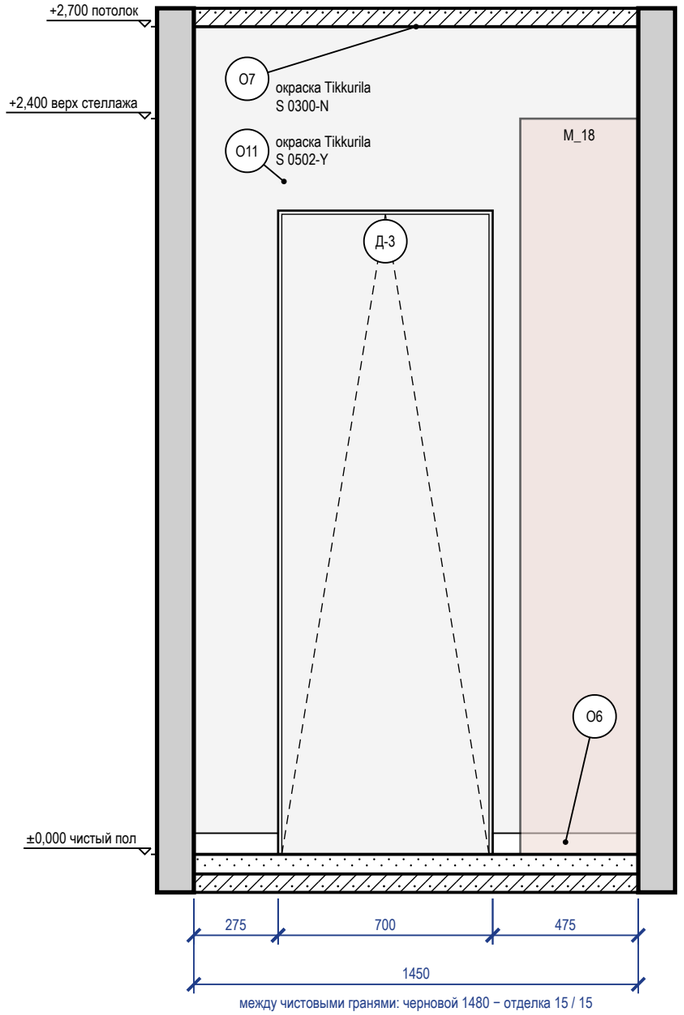


между чистовыми гранями: черновой 1480 − отделка 15 / 15

Развёртка стены Б

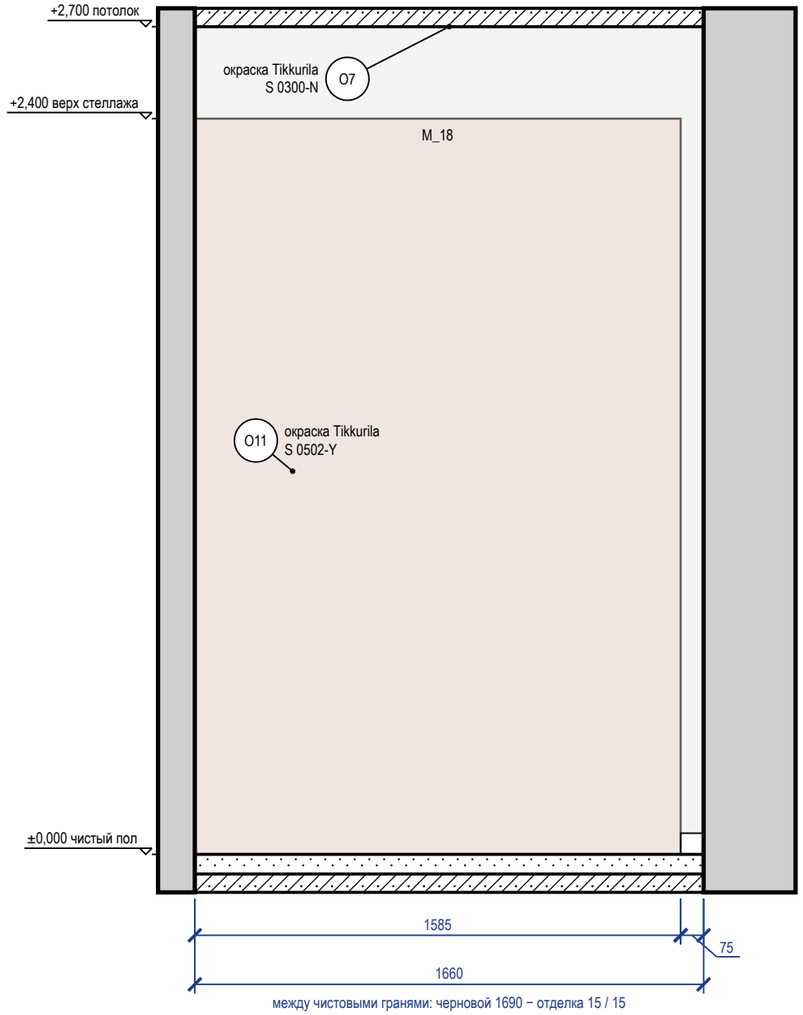


между чистовыми гранями: черновой 1690 − отделка 15 / 15

Развёртка стены В

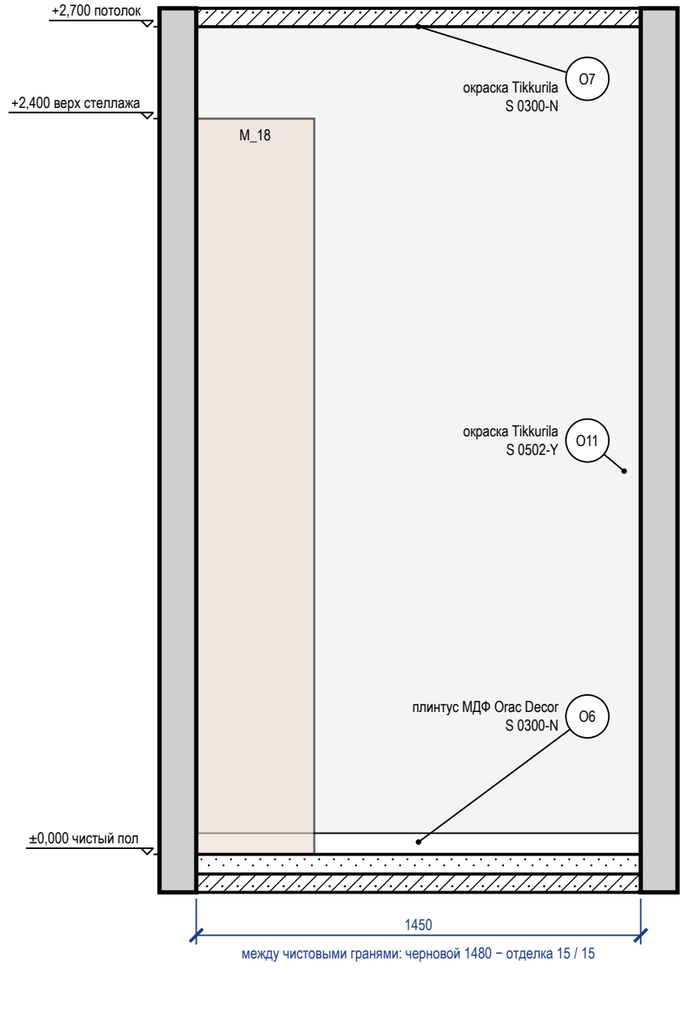

между чистовыми гранями: черновой 1480 − отделка 15 / 15

Схема развёрток (М 1:100)

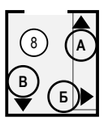

Ведомость отделки (на листе)

Марка	Поверхность	Материал, изделие	Цвет, код	Кол.
О6	плинтус	плинтус МДФ, Orac Decor Contour (Luxxus), h 69 мм, SX165, шелковисто-матовая	NCS S 0300-N	2,3 м
О7	потолок	окраска, Tikkurila, глубокоматовая	NCS S 0300-N	2,5 м²
О11	стены	окраска, Tikkurila, матовая, подготовка Q3	NCS S 0502-Y	10,8 м²

Примечания

1. Размеры — в мм от чистовых поверхностей стен; условные обозначения и общие указания — лист 3.
2. Двери скрытого монтажа — полотно в плоскости стены, отделка стены по полотну, плинтус прерывается у короба (узел — на листе узлов).

					Проект: Квартира 65 м² — М 1:20
	Лист	№ док.	Подпись	Дата	Развёртки стен. Кладовая (пом. 8)
Дизайнер	Кырлан А.С.			04.11.26	Стадия: П; Лист: 65; Листов: 83

Развёртка стены А


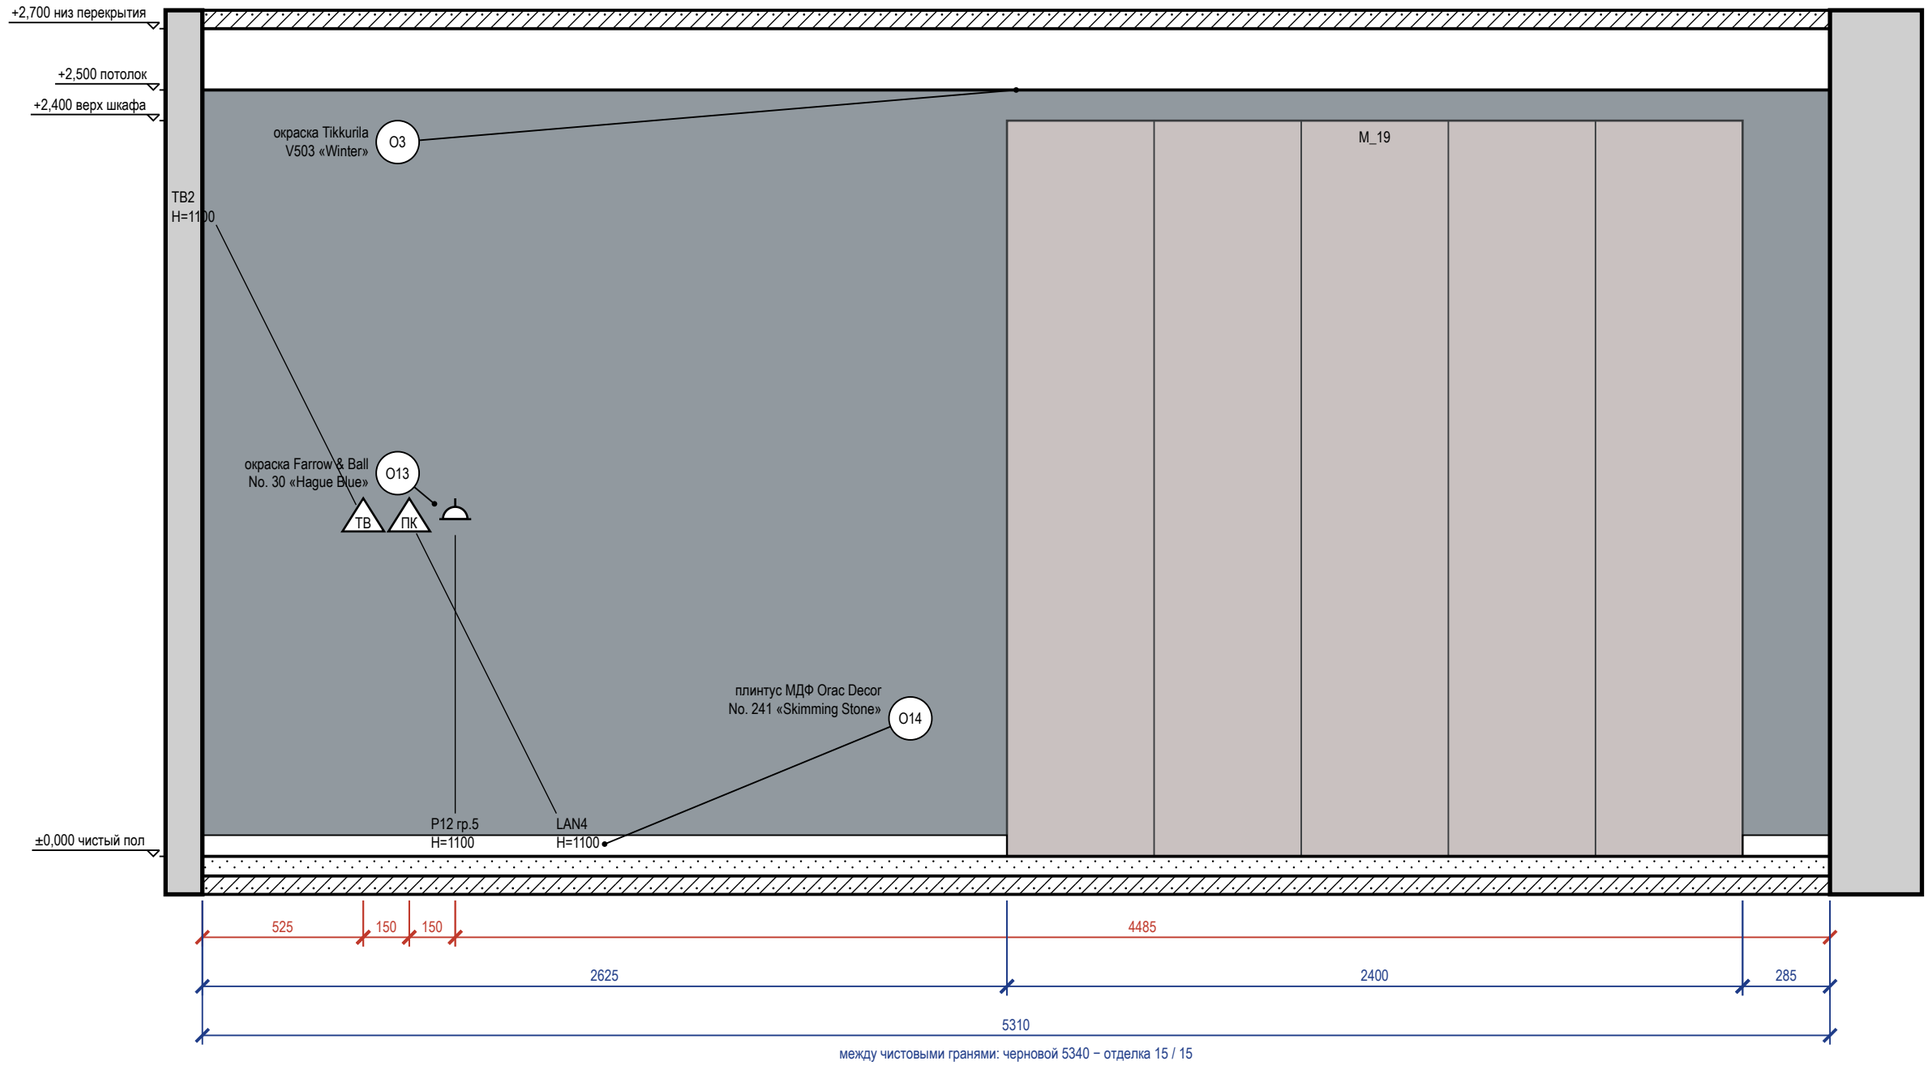


Схема развёрток (М 1:100)

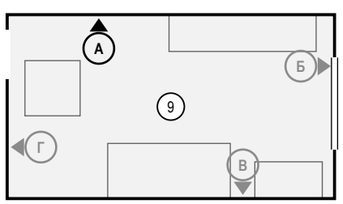

Ведомость отделки (на листе)

Марка	Поверхность	Материал, изделие	Цвет, код	Кол.
О3	потолок	окраска, Tikkurila Anti-Reflex 2, глубокоматовая, подготовка Q3	Tikkurila V503 «Winter»	16 м²
О13	акцентная стена	окраска, Farrow & Ball Modern Emulsion, матовая, подготовка Q3	Farrow & Ball No. 30 «Hague Blue»	13,3 м²
О14	плинтус	плинтус МДФ, Orac Decor Contour (Luxxus), h 69 мм, SX165	Farrow & Ball No. 241 «Skimming Stone»	2,9 м

Примечания

1. Размеры — в мм от чистовых поверхностей стен; условные обозначения и общие указания — лист 3.
2. Потолок — у каждой стены свой, по плану потолков (ПТ3); ступени — зоной, кромка короба перед нишей — тонкой линией; в поле потолка: ПТ1 +2,600.

	Лист	№ док.	Подпись	Дата
Дизайнер	Кырлан А.С.			04.11.26

Проект: Квартира 65 м² — М 1:20

Развёртка стены А. Детская (пом. 9)

Стадия	Лист	Листов
П	66	83

Развёртка стены Б


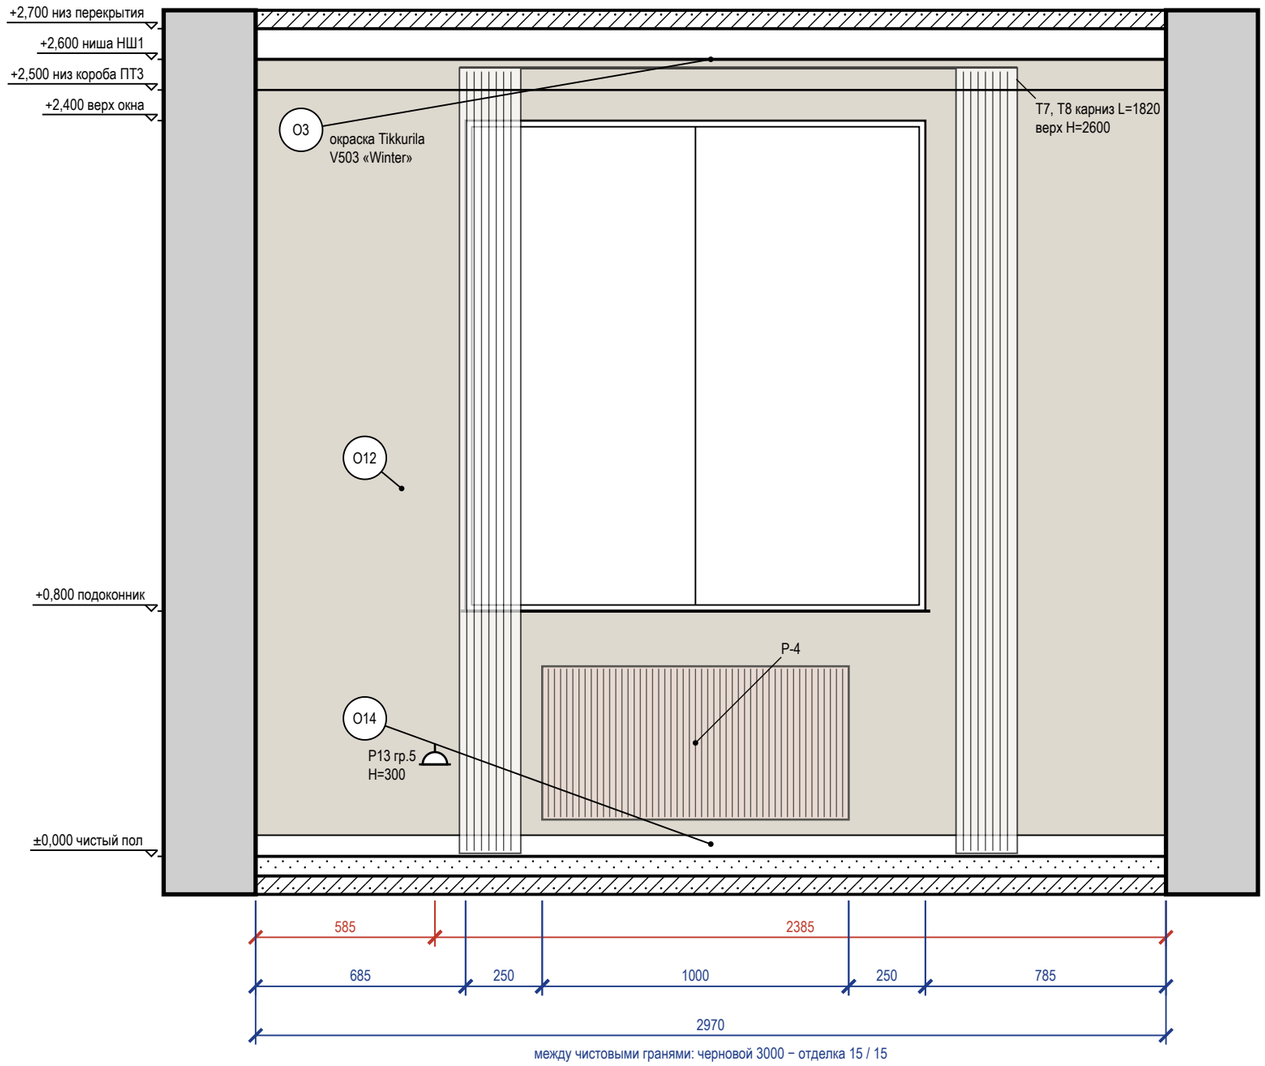


Схема развёрток (М 1:100)

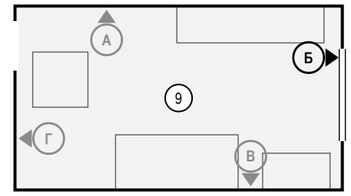

Ведомость отделки (на листе)

Марка	Поверхность	Материал, изделие	Цвет, код	Кол.
О3	потолок	окраска, Tikkurila Anti-Reflex 2, глубокоматовая, подготовка Q3	Tikkurila V503 «Winter»	16 м²
О12	стены	окраска, Farrow & Ball Modern Emulsion, матовая, подготовка Q3	Farrow & Ball No. 241 «Skimming Stone»	5,3 м²
О14	плинтус	плинтус МДФ, Orac Decor Contour (Luxxus), h 69 мм, SX165	Farrow & Ball No. 241 «Skimming Stone»	3 м

Примечания

1. Размеры — в мм от чистовых поверхностей стен; условные обозначения и общие указания — лист 3.
2. Карнизы (шины) — по ведомости текстиля декоратора: длина L и верх H на развёртке — те же числа, что в ведомости; крепление — до окраски потолка.
3. Потолок — у каждой стены свой, по плану потолков (НШ1, ПТ3); ступени — зоной, кромка короба перед нишей — тонкой линией; в поле потолка: ПТ1 +2,600.

					Проект: Квартира 65 м² — **М 1:20**
	Лист	№ док.	Подпись	Дата	Развёртка стены Б. Детская (пом. 9)
Дизайнер	Кырлан А.С.			04.11.26	Стадия: П · Лист: 67 · Листов: 83

Развёртка стены В


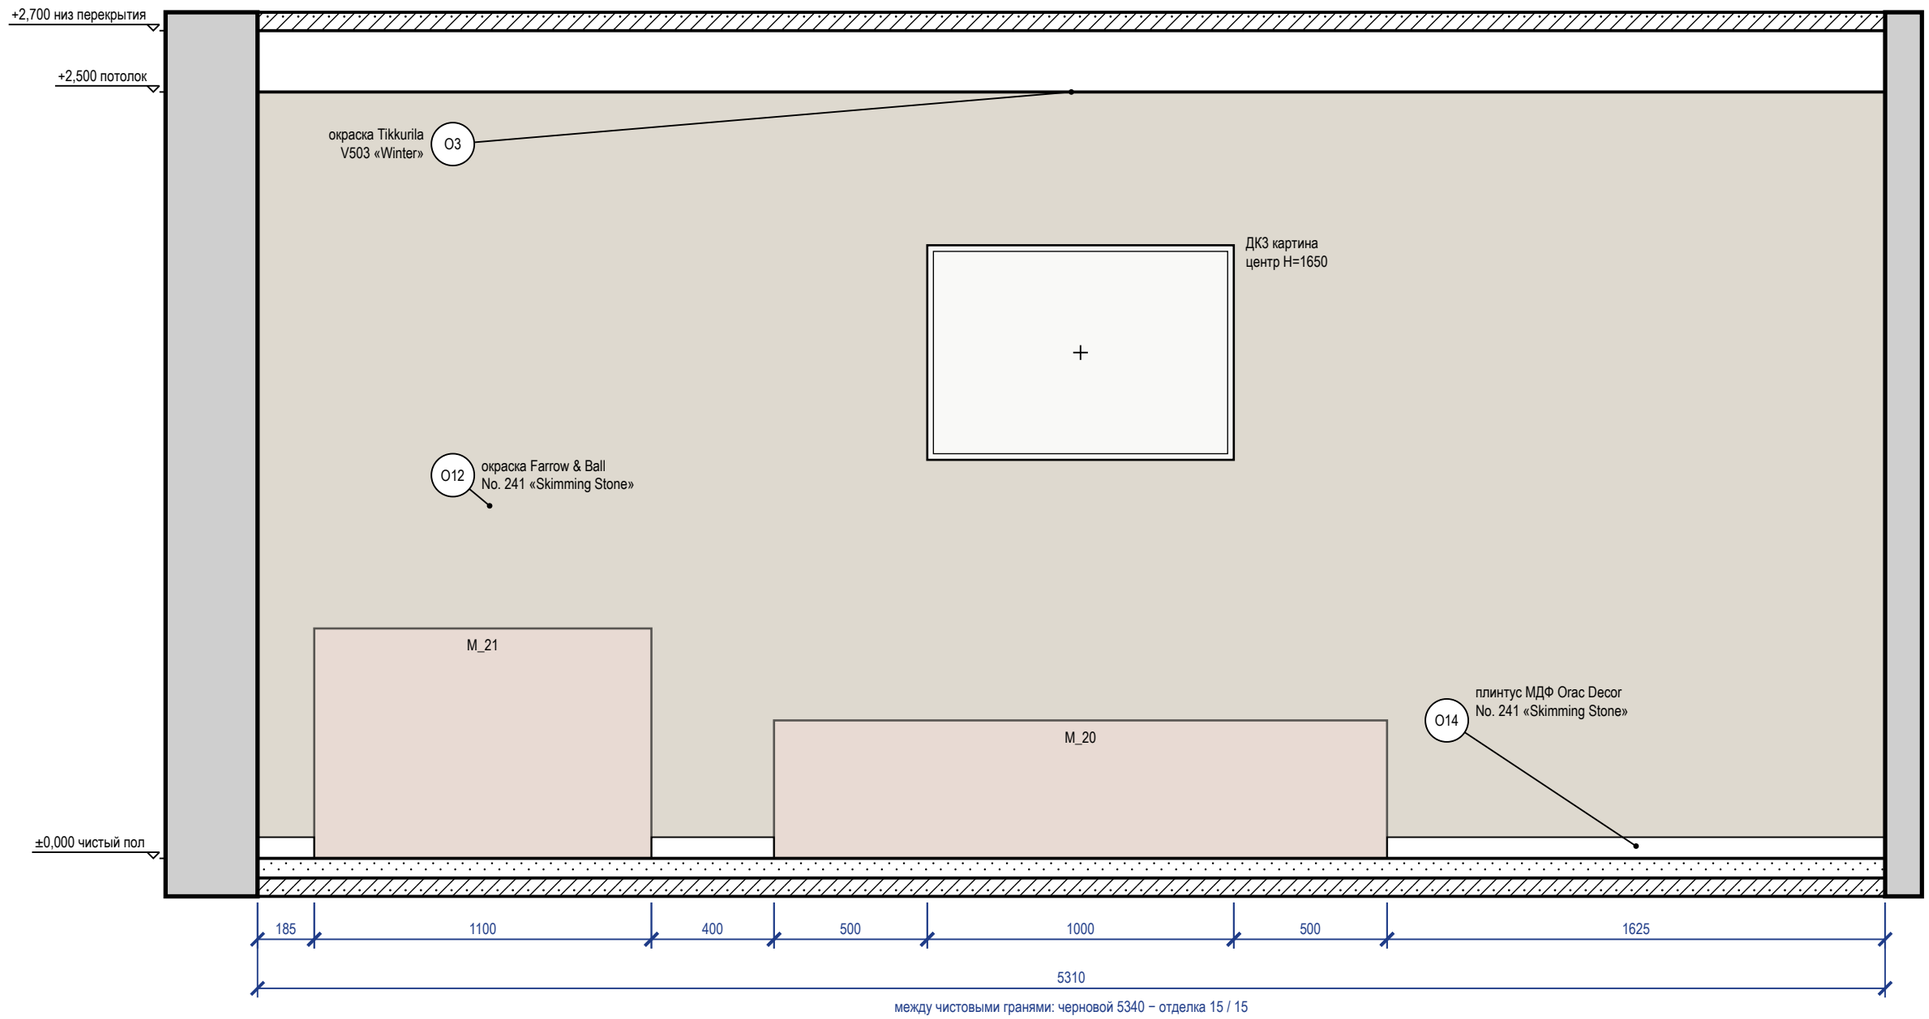


Схема развёрток (М 1:100)

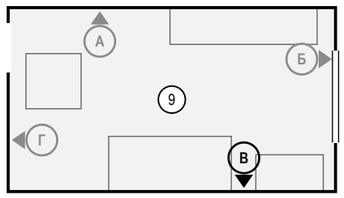

Ведомость отделки (на листе)

Марка	Поверхность	Материал, изделие	Цвет, код	Кол.
О3	потолок	окраска, Tikkurila Anti-Reflex 2, глубокоматовая, подготовка Q3	Tikkurila V503 «Winter»	16 м²
О12	стены	окраска, Farrow & Ball Modern Emulsion, матовая, подготовка Q3	Farrow & Ball No. 241 «Skimming Stone»	13,3 м²
О14	плинтус	плинтус МДФ, Orac Decor Contour (Luxxus), h 69 мм, SX165	Farrow & Ball No. 241 «Skimming Stone»	2,2 м

Примечания

1. Размеры — в мм от чистовых поверхностей стен; условные обозначения и общие указания — лист 3.
2. Стена В показана двумя видами: здесь — архитектурная развёртка (мебель, отделка, проёмы, высоты), электроточки и выводы ВК с привязками и таблицей — на листе 69 («Привязки»).
3. Картины и зеркала крепить к основанию по паспорту изделия (закладные и анкеры — в перечне скрытых работ); крест — ось центра предмета.
4. Потолок — у каждой стены свой, по плану потолков (ПТ3); ступени — зоной, кромка короба перед нишей — тонкой линией; в поле потолка: ПТ1 +2,600.

					Проект: Квартира 65 м²	М 1:20
	Лист	№ док.	Подпись	Дата		
Дизайнер	Кырлан А.С.			04.11.26	Развёртка стены В. Детская (пом. 9)	

Стадия	Лист	Листов
П	68	83

Развёртка стены В: электроточки и выводы

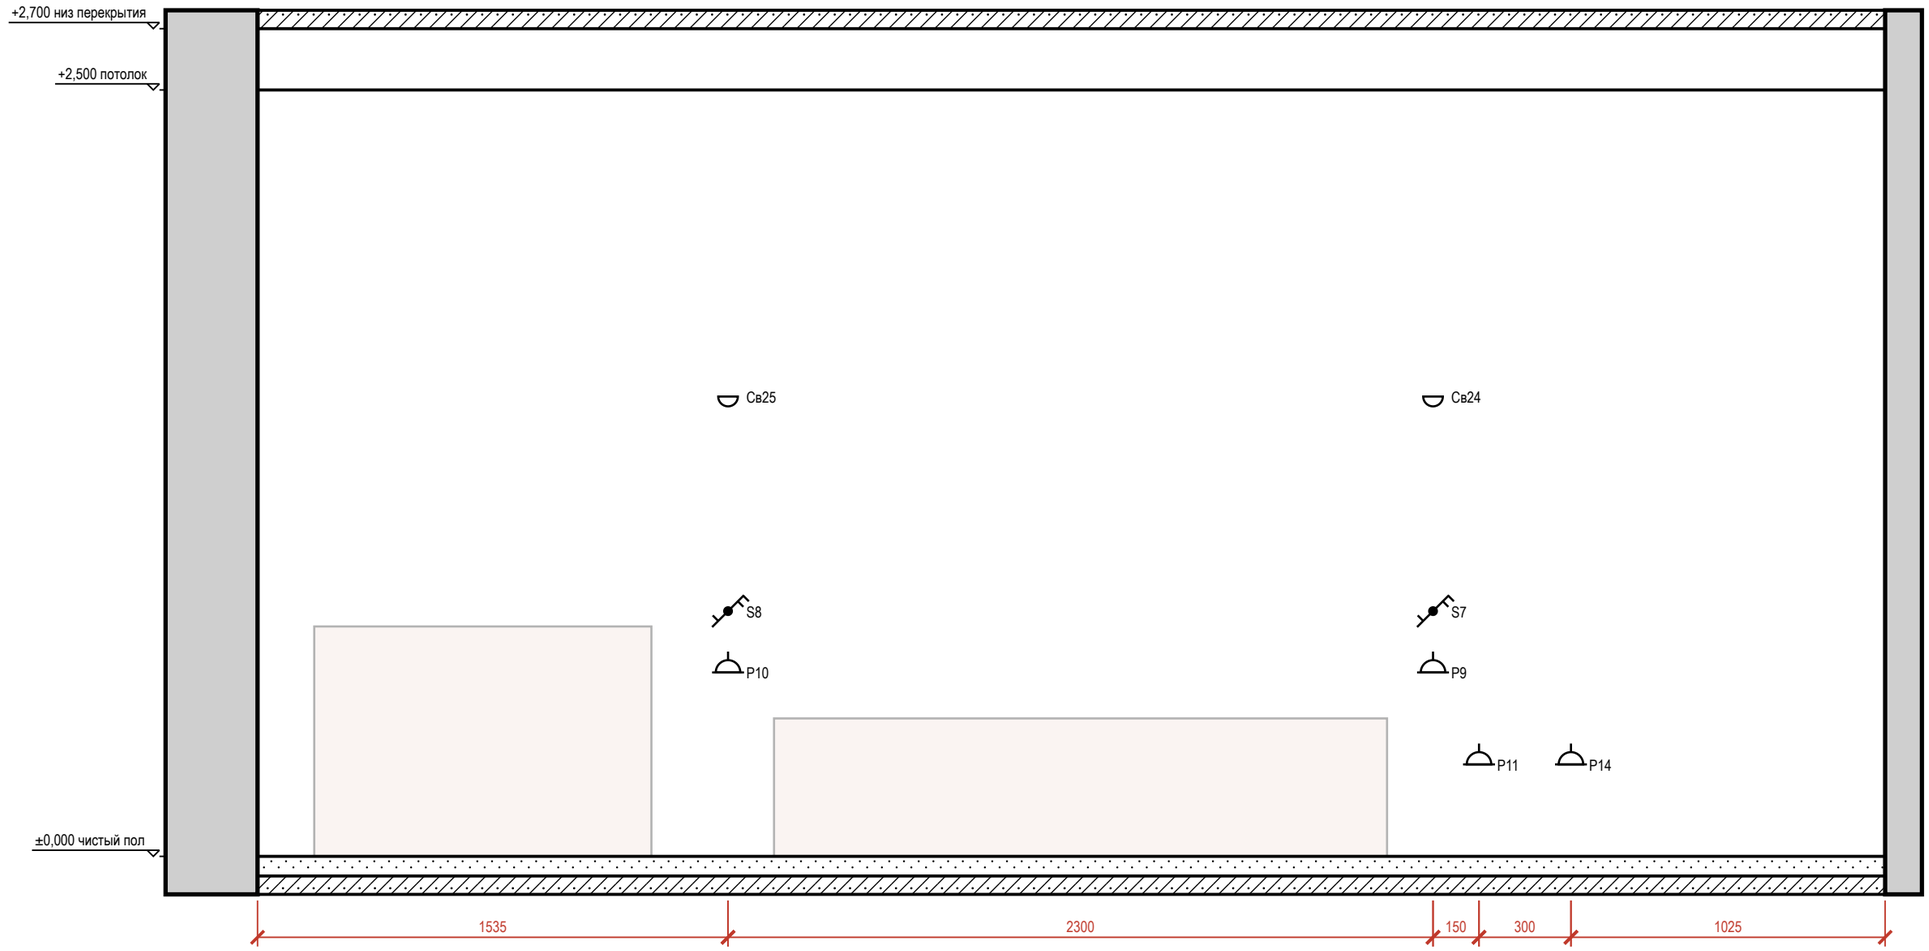



Таблица привязок электроточек и выводов

Марка	Назначение	От угла, мм	Н от пола, мм	Примечание
P10	розетка: у кровати	1535	600	гр. 5
S8	выключатель	1535	800	гр. 1
Св25	светильник настенный	1535	1500	гр. 1
P9	розетка: у кровати	3835	600	гр. 5
S7	выключатель	3835	800	гр. 1
Св24	светильник настенный	3835	1500	гр. 1
P11	розетка: торшер у кровати M_20 (изголовье)	3985	300	гр. 5
P14	розетка: уборка у входа	4285	300	гр. 5

Условные обозначения

- розетка с заземляющим контактом; у знака — марка, ×N постов в рамке, гр. — группа щита, Н — высота оси, мм
- выключатель одноклавишный
- выключатель двухклавишный (флажков — по числу клавиш)
- выключатель с проходной или перекрёстной клавишей (обратный флажок); тип клавиши — в подписи
- светильник настенный (бра), Н — высота оси
- привязки точек и выводов от угла и от пола, мм
- А — марка развёртки: буква стены, стрелка — взгляд

Схема развёрток (М 1:100)

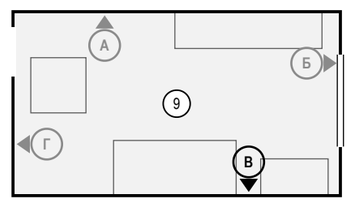

Примечания

1. Вид «Привязки» стены В — электроточки и выводы ВК; архитектурная развёртка (мебель, отделка, проёмы, высоты) — на листе 68. Мебель и приборы — подложкой для ориентира; их марки и обозначения мебели, проёмов и стен — там же.
2. Привязки — в мм: по горизонтали от левого чистового угла стены до оси изделия, Н — от чистого пола до оси; все точки — в таблице привязок. Красная цепочка — привязки по осям; точки ближе 120 мм одна к другой в цепочку не дробятся — их привязки только в таблице.
3. У знака — марка электроточки (Р — розетка, S — выключатель, Св — светильник, ЭВ — вывод кабеля); условные обозначения и общие указания — лист 3.

	Лист	№ док.	Подпись	Дата
Дизайнер	Кырлан А.С.			04.11.26

Проект: Квартира 65 м² — М 1:20

Привязки электроточек, стена В. Детская (пом. 9)

Стадия	Лист	Листов
П	69	83

Развёртка стены Г


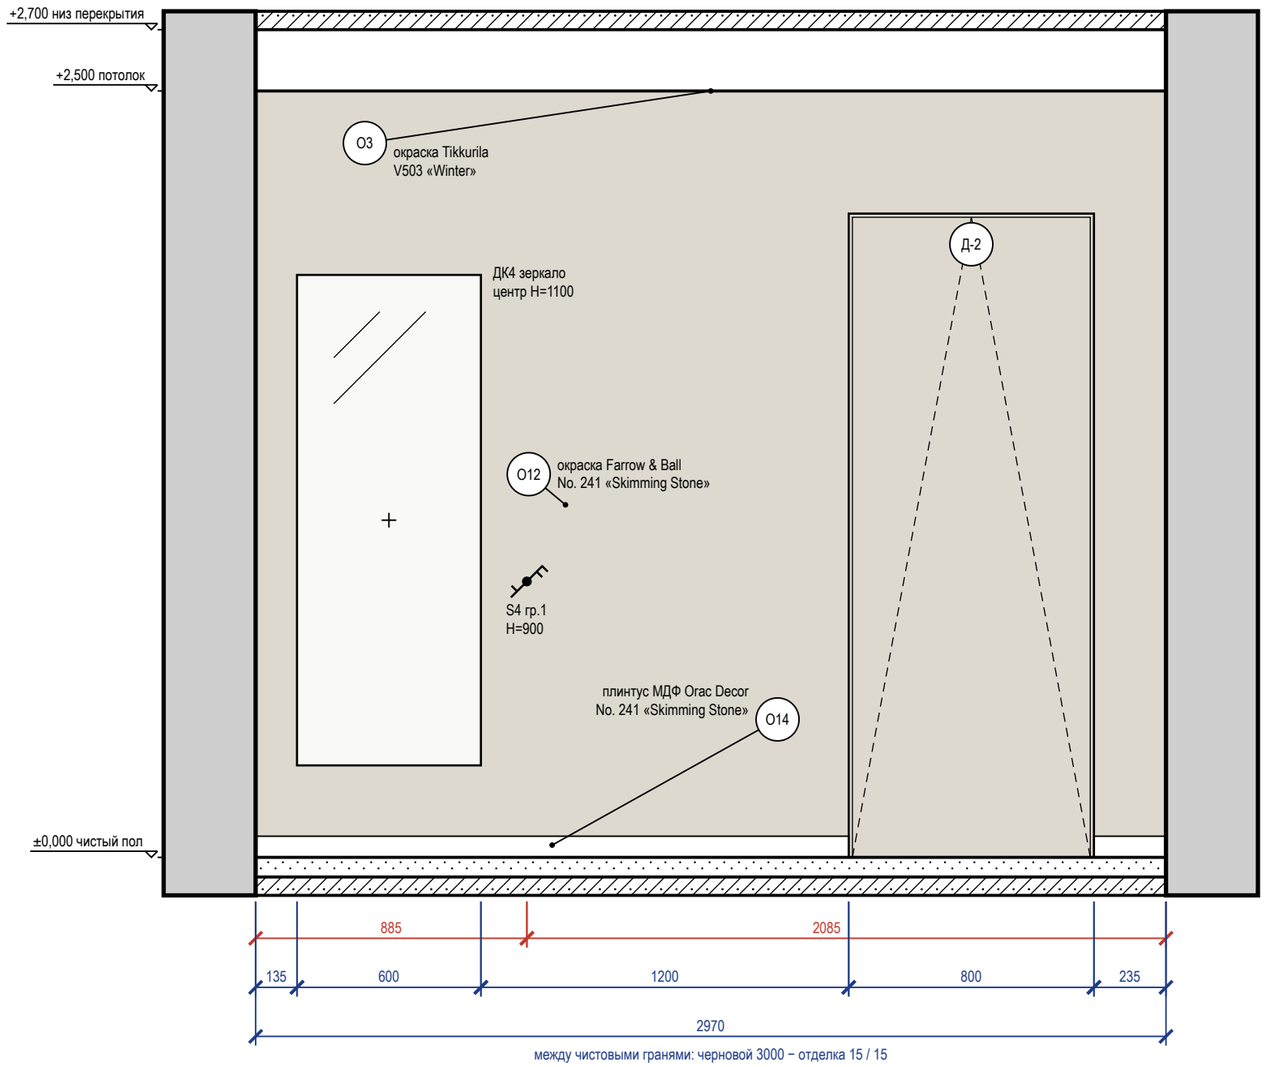


Схема развёрток (М 1:100)

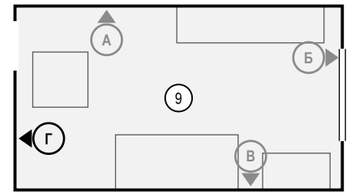

Ведомость отделки (на листе)

Марка	Поверхность	Материал, изделие	Цвет, код	Кол.
О3	потолок	окраска, Tikkurila Anti-Reflex 2, глубокоматовая, подготовка Q3	Tikkurila V503 «Winter»	16 м²
О12	стены	окраска, Farrow & Ball Modern Emulsion, матовая, подготовка Q3	Farrow & Ball No. 241 «Skimming Stone»	5,7 м²
О14	плинтус	плинтус МДФ, Orac Decor Contour (Luxxus), h 69 мм, SX165	Farrow & Ball No. 241 «Skimming Stone»	2,2 м

Примечания

1. Размеры — в мм от чистовых поверхностей стен; условные обозначения и общие указания — лист 3.
2. Картины и зеркала крепить к основанию по паспорту изделия (закладные и анкеры — в перечне скрытых работ); крест — ось центра предмета.
3. Двери скрытого монтажа — полотно в плоскости стены, отделка стены по полотну, плинтус прерывается у короба (узел — на листе узлов).
4. Потолок — у каждой стены свой, по плану потолков (ПТ3); ступени — зоной, кромка короба перед нишей — тонкой линией; в поле потолка: ПТ1 +2,600.

					Проект: Квартира 65 м²	М 1:20
	Лист	№ док.	Подпись	Дата		
Дизайнер	Кырлан А.С.			04.11.26	Развёртка стены Г. Детская (пом. 9)	

Стадия	Лист	Листов
П	70	83

Комплект предварительный по пунктам этих таблиц. Пока по пункту нет ответа или решения, показанное на указанном листе — допущение проектировщика, а не утверждённое решение.
Сводка: открытых вопросов — 11 (из них ждут факта объекта — 5: контрольного обмера, обследования или документа); изменений в реестре — 1, из них без подписи — 1.

Открытые вопросы и принятые допущения

№	Формулировка	Вид	Кто решает	Если решения нет	Лист, где это проявляется
К-1	Размеры квартиры сняты с растрового плана заказчика без размерных цепочек: масштаб восстановлен по подписанным площадям помещений. До заказа мебели, дверей и материалов нужен контрольный обмер всех помещений и проёмов.	Отсутствует Ждёт: обмера	Архитектор-планировщик	размеры на листах — по плану заказчика, уточняются по месту; мебель на заказ и материалы по ним не заказывать	л. 5 — План планировки от заказчика л. 11 — План размещения мебели и оборудования
К-2	Высота потолка на плане заказчика не указана, принята 2700 мм.	Отсутствует	Архитектор-планировщик	высоты на развёртках и потолки — от 2700 мм, уточнить при обмере	л. 5 — План планировки от заказчика л. 28 — План потолков
К-3	Спальня (пом. 2) по плану заказчика без окна: жилая комната должна иметь естественное освещение (СП 54.13330.2022). Нужно решение заказчика: перенести спальню к окну, дать окно или назначить помещение нежилым (гардеробная, кабинет). По плану заказчика спальня отделена от гостиной остеклённой перегородкой на подиуме +0,550 (второй свет), окна в наружной стене А нет: окно в данные не вносится (факт объекта), помещение остаётся «Спальня» до решения заказчика; ошибка на листе стоит сознательно.	Спорно Ждёт: решения	Архитектор-планировщик	помещение не может быть принято как жилая комната; планировка на согласование не подаётся	л. 5 — План планировки от заказчика л. 11 — План размещения мебели и оборудования
К-4	Разрешённая мощность квартиры по ТУ неизвестна, принята 15 кВт.	Отсутствует	Инженер-электрик	щит и группы рассчитаны на 15 кВт; при меньших ТУ пересчёт	л. 32 — Однолинейная схема щита л. 33 — План розеток и электровыводов
К-5	Кухня-гостиная (пом. 3): диван M_07 2200 × 950 стоит в полосе 1400 мм между спальней и кухней — единственном проходе от двери из коридора в комнату; за спинкой остаётся щель 290 мм, в выпуске для заказчика это ошибка. Полоса годится только под проход и неглубокую мебель (до 700 мм). В основной части (2700 × 2900 мм) диван, обеденная группа на 4 места, рабочее место M_08 и кресло M_06 вместе с проходами не помещаются. Нужно решение по составу зоны: (1) диван в основную часть лицом к ТВ на стене Г, обеденный стол — в нишу у колонны M_13, рабочее место M_08 — в спальню или детскую; (2) диван двухместный 1600 мм у стены спальни в основной части; (3) вместо обеденной группы — барная стойка. До решения расстановка кухни-гостиной не годится для заказа мебели. Решение исполнителя (ИЗ-1, 30.10.2026, на утверждение автора): вариант 1 без переноса рабочего места диван M_07 у стены А основной части (x 250…2450, y 1650…2600), обеденный стол M_05 перед ним (x 1100…2100, y 2800…3800), кресло M_06 у окна 2 (x 400…1150, y 3700…4450), ТВ остаётся на стене Г; полоса 1400 у спальни свободна под проход; части 2–4 помещения перекроены (кухонный ряд и ниша — одна часть) без изменения контура. Стыки частей ≥ 700 мм.	Спорно Ждёт: решения	Дизайнер интерьера	расстановка M_07, M_05, M_06 остаётся предложением со знаком «**»: мебель кухни-гостиной не заказывать до подписи ИЗ-1	л. 11 — План размещения мебели и оборудования
К-6	Спальня (пом. 2) без окна (К-3): приток не решён — бризер на внутренней стене Б не работает (нужно отверстие в наружной стене), а наружная стена А занята изголовьем кровати M_02 (бризер над кроватью — холодный поток на спящего). Радиатор Р-2 оставлен на стене Б у двери. После решения по окну: бризер или клапан — у окна, радиатор — под окно; если помещение станет нежилым приток не нужен.	Решение	Инженер ОВ	приток в спальню не обеспечен: на плане вентиляции «!» в графе притока; радиатор Р-2 — на стене Б	л. 38 — План вентиляции л. 39 — План отопления
К-7	Вентканалы на плане заказчика не показаны: ВК-1 и ВК-2 приняты проектировщиком у кухни, ванная (пом. 7) от них далеко вытяжка ВР3 идёт воздуховодом ≈ 4 м через санузел. Замерить положение и сечение каналов; если канал у ванной есть — решётку в его стенку, воздуховод не нужен.	Отсутствует Ждёт: обмера	Инженер ОВ	вытяжка ванной — вентилятором с обратным клапаном и воздуховодом под потолком до ВК-2; места решёток — до обмера	л. 38 — План вентиляции
К-8	Проём санузла (пом. 6, марка Д-5) по плану заказчика 550×2100 — уже ряда стандартных полотен (600–900): полотно ≈ 450 под заказ, проход меньше 600. Откос от угла коридора до проёма — 40 мм, под коробку нужно не меньше 50. Проём в существующей стене: расширить до 700 (полотно 600) можно только при подтверждении, что стена не несущая (техзаключение / план БТИ). Замерить проём в чистоте и откос; решить — расширение по техзаключению или изделие под заказ.	Спорно Ждёт: обмера, затем решения	Архитектор-планировщик	Д-5 — скрытая дверь под заказ по проёму 550×2100 (полотно ≈ 450), проём не расширяется; заказ — только после замера в чистоте	л. 27 — План размещения дверей
К-9	Климатический подрайон (СП 131.13330) не задан: принят не северный — жилые комнаты и кухня под потолком от 2,5 м (СП 54, п. 5.12); в IA, IБ, IГ, IД, IVA — от 2,7 м.	Отсутствует Ждёт: документа	Архитектор-планировщик	отметки потолков жилых — по 2,5 м; при северном подрайоне уровни ниже 2,7 м пересчитать до заказа каркаса	л. 28 — План потолков
К-10	Несущие стены не определены: плана БТИ, проекта дома и технического заключения в материалах объекта нет. До их получения все существующие стены считаются несущими — демонтаж, новые проёмы и штробы в них не планируются. Нужно: запросить план БТИ и проект дома, установить серию и материал стен; несущие стены и допустимость вмешательства определяет техническое заключение специализированной организации.	Отсутствует Ждёт: документа	Архитектор-планировщик	все существующие стены — несущие: перепланировка и штробы в них не выполняются, на листах обмера и демонтажа — «не определены, считать несущими»	л. 5 — План планировки от заказчика полный альбом
К-12	Циркуляция ГВС в данных не задана — циркуляционного трубопровода на схеме нет. Решить: нужна ли циркуляция	Отсутствует Ждёт: решения	Инженер ВК (вода, канализация)	циркуляции на схеме нет	л. 20–22 — Развёртки мокрых зон: выводы ВК. Кухня-гостиная л. 17 — Аксонометрическая схема В1 (холодное водоснабжение) л. 16 — Схема разводки водопровода и канализации

					Проект: Квартира 65 м²
	Лист	№ док.	Подпись	Дата	Открытые вопросы, принятые допущения и конфликты. Лист 1 из 2
Дизайнер	Кырлан А.С.			04.11.26	

Стадия	Лист	Листов
П	71	83

Изменения проекта после выпуска листов (реестр изменений)


№	Дата	Лист	Было	Стало	Кто решил, подпись
ИЗ-1	30.10.2026	л. 11 — План размещения мебели и оборудования л. 12 — Спецификация мебели и оборудования л. 33 — План розеток и электровыводов л. 49 — Развёртка стены В. Кухня-гостиная (пом. 3), кухонный фронт	Кухня-гостиная (пом. 3): диван M_07 2200×950 стоял в полосе 1400 мм между спальней и кухней (x 2900…5100, y 3000…3950) — единственном проходе от двери Д-2; стыки частей 0–1 — 290 мм, 1–3 — 200, 1–4 — 0, 2–3 — 600; кресло M_06 в x 800, стол M_05 в x 1000, y 2700. Вопрос К-5 открыт.	Диван M_07 у стены А основной части (x 250…2450, y 1650…2600), стол M_05 перед ним (x 1100…2100, y 2800…3800), кресло M_06 у окна 2 (x 400…1150, y 3700…4450); розетки «у дивана» перенесены на стену А (x 700, 2300), розетка торшера — на стену Г (offset 1900). Части помещения 2–4 перекроены без изменения контура: кухонный ряд M_09, M_10, M_11, M_12, M_13 и ниша M_08 — одна часть (0…4850 × 4550…5800), связка 2700…4850 × 4050…4550; стык частей 2–3 проходил сквозь кухонный ряд (600 мм — глубина столешницы, не проход). Знак «**» у M_07, M_05, M_06 до подписи автора; К-5 — у автора.	Не утверждено: подписи нет. решение исполнителя; предложение проектировщика, на утверждение А. С. Кырлана

Примечания


1. Номера листов — по ведомости рабочих чертежей комплекта (лист «Общие данные»).
2. Графа «Если решения нет» показывает состояние решения на листах; влияние на сроки и стоимость по пунктам не оценивалось.
3. Пункт, по которому принято решение, при следующем выпуске комплекта из таблиц исключается.

					Проект: Квартира 65 м²		
	Лист	№ док.	Подпись	Дата	Открытые вопросы, принятые допущения и конфликты. Лист 2 из 2	Стадия	Лист	Листов
Дизайнер	Кырлан А.С.			04.11.26		П	72	83


Общий вид

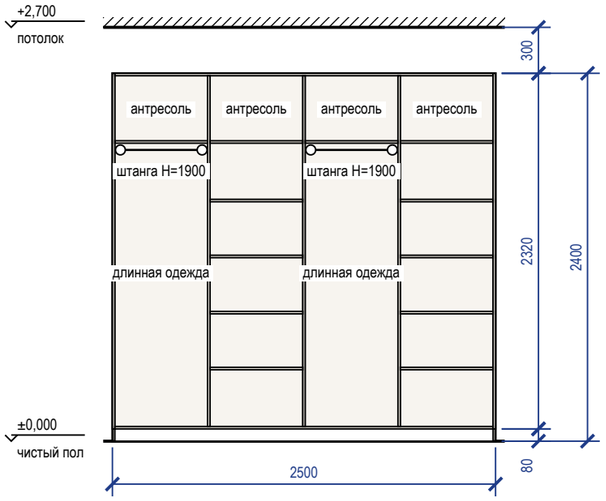


Наполнение, размеры в свету

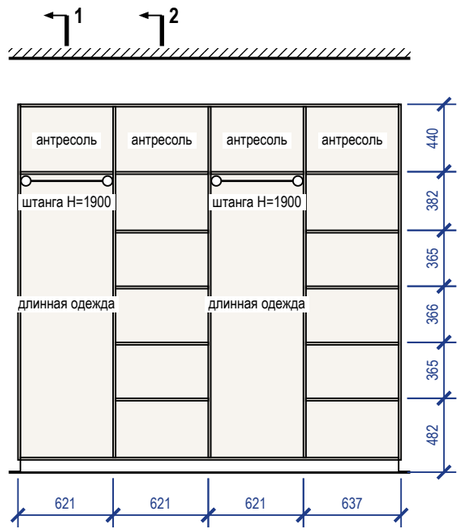

Разрез 1-1

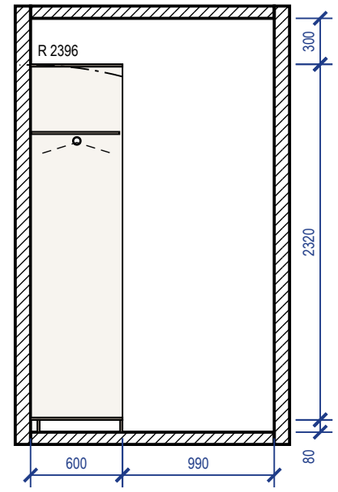

Разрез 2-2

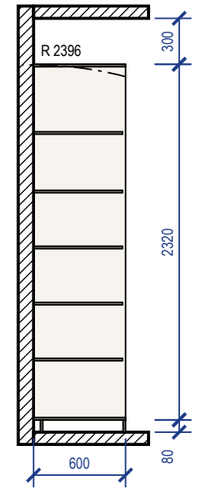


Примечания

1. Размеры — в мм по чистовой отделке; изделие 2500×600×2400 (Ш×Г×В). Перед раскроем — контрольный замер цеха после чистовой отделки стен, пола и потолка.
2. Корпус — ЛДСП 16 мм, задняя стенка ХДФ 4 мм в паз, цоколь 80 мм на регулируемых опорах; открытая система: без фасадов.
3. Кромка: скрытые торцы 0,4 мм, видимые 2 мм (ПВХ/АБС).
4. Присадка по 32-й системе — выполняет цех.
5. Зазор до потолка 300 мм.
6. Подъём корпуса: диагональ боковины без цоколя $\sqrt{(2320^2 + 600^2)}$ = 2396 мм < 2700 мм до потолка — корпус собирается лёжа, поднимается поворотом и ставится на цоколь.
7. Крепление к стене от опрокидывания: крепление к стене, 3 точки; основание стены и шаг анкеров — монтажная схема шкафов.
8. Проход перед изделием 990 мм показан на разрезе 1-1.


3D орто

					Проект: Квартира 65 м²	**М 1:40**
	Лист	№ док.	Подпись	Дата		
Дизайнер	Кырлан А.С.			04.11.26	Система хранения М_01	Стадия: П; Лист: Д_1; Листов: 83


Вид с фасадами

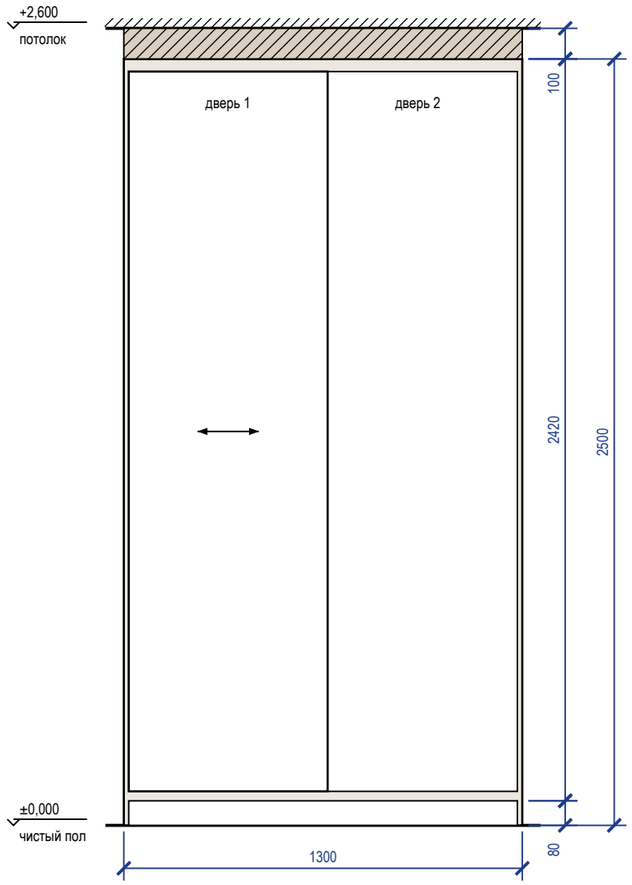


Вид без фасадов

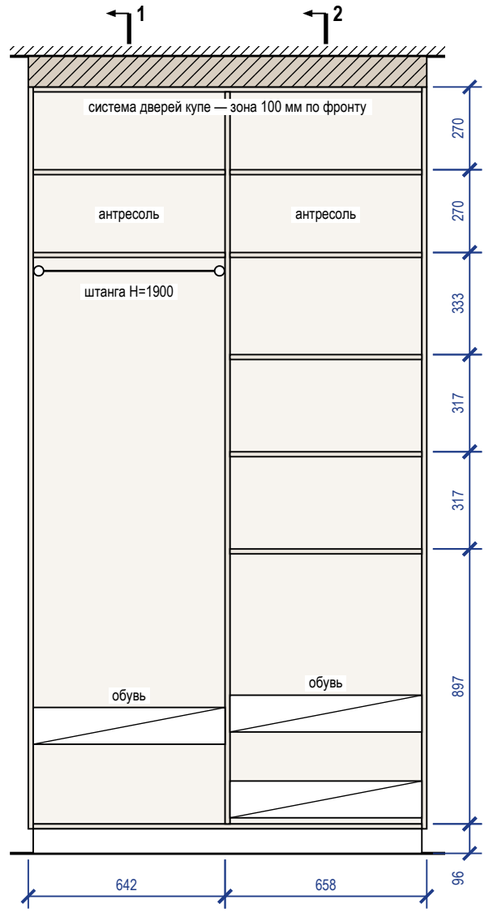

Разрез 1-1

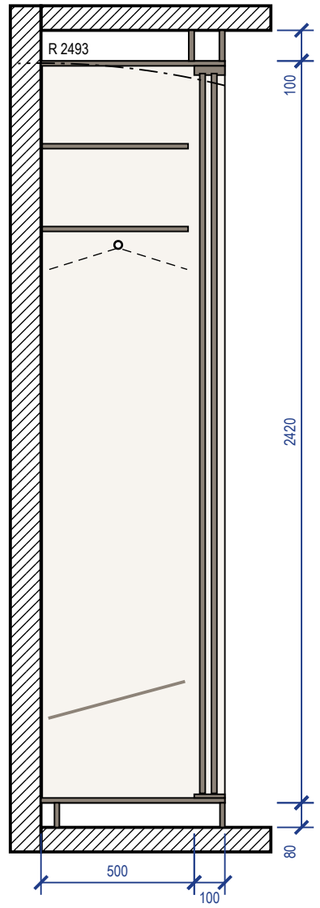


Разрез 2-2

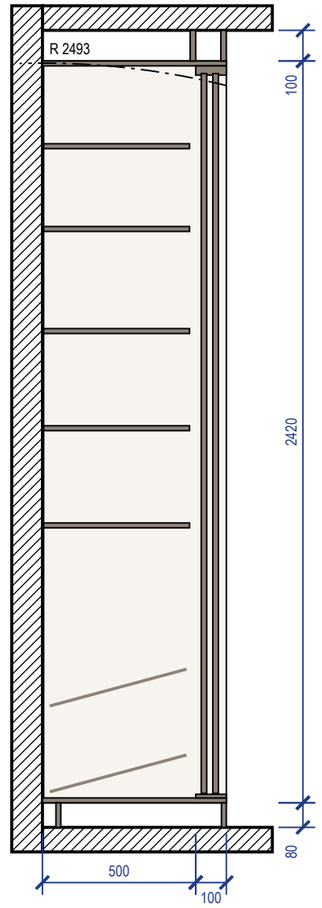

Примечания


1. Размеры — в мм по чистовой отделке; изделие 1300×600×2500 (Ш×Г×В). Перед раскроем — контрольный замер цеха после чистовой отделки стен, пола и потолка.
2. Корпус — ЛДСП 16 мм, задняя стенка ХДФ 4 мм в паз, цоколь 80 мм на регулируемых опорах; двери купе — ЛДСП 10 мм в алюминиевом профиле; нахлёст 30 мм, ширина двери 649 мм, высота — проём минус 40 мм; цвет — по колерной карте.
3. Кромка: скрытые торцы 0,4 мм, видимые 1 мм (ПВХ/АБС).
4. Номинальные зазоры: дверь купе — боковина 3 мм, фасад ящика — стойка 2 мм; ящики внутри купе — с накладкой 30 мм на стойке со стороны нахлёста дверей.
5. Присадка по 32-й системе — выполняет цех.
6. Компенсатор 100 мм — короб из ЛДСП по фронту и торцам, подгоняется к потолку при монтаже (припуск 20 мм), крепится к корпусу и к потолку.
7. Подъём корпуса: диагональ боковины без цоколя $\sqrt{(2420^2 + 600^2)} = 2493$ мм < 2600 мм до потолка — корпус собирается лёжа, поднимается поворотом и ставится на цоколь.
8. Крепление к стене от опрокидывания — уголки 2 шт. к несущему основанию (монтажная схема шкафов).

3D орто

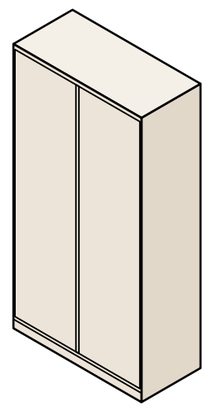


					Проект: Квартира 65 м²		M 1:20
	Лист	№ док.	Подпись	Дата			
Дизайнер	Кырлан А.С.			04.11.26	Шкаф-купе M_17	Стадия	Лист	Листов
						П	Д_2	83


Общий вид

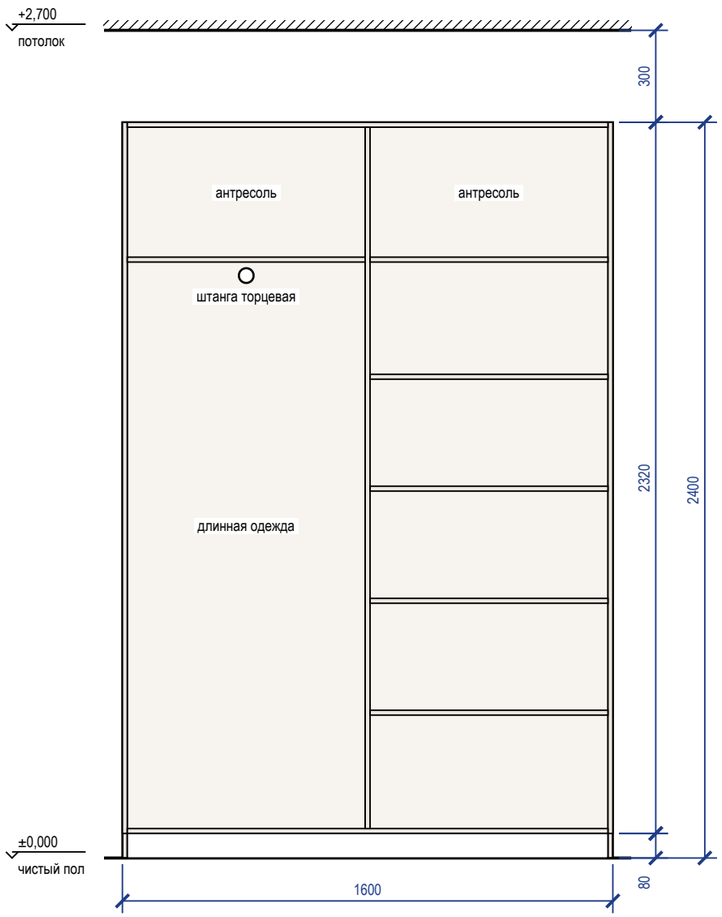


Наполнение, размеры в свету

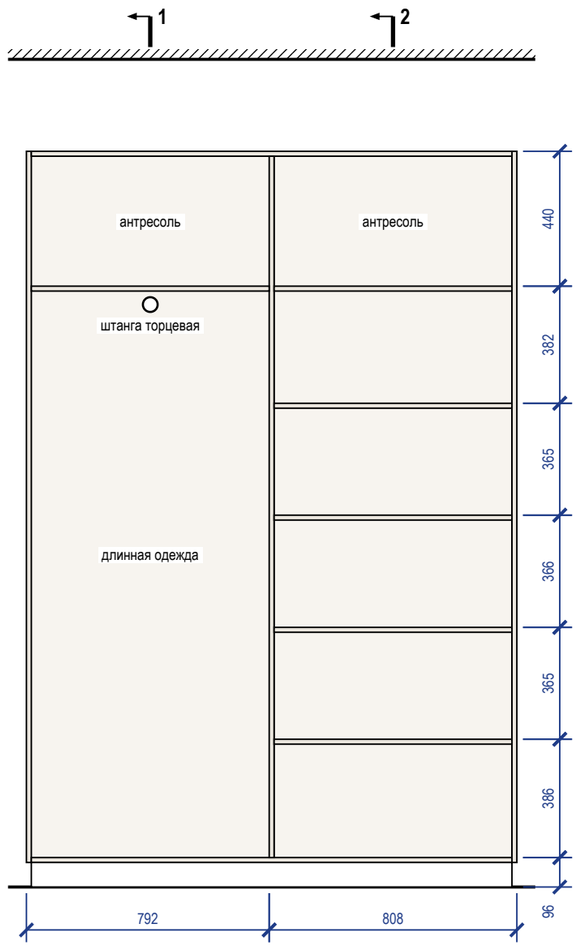

Разрез 1-1

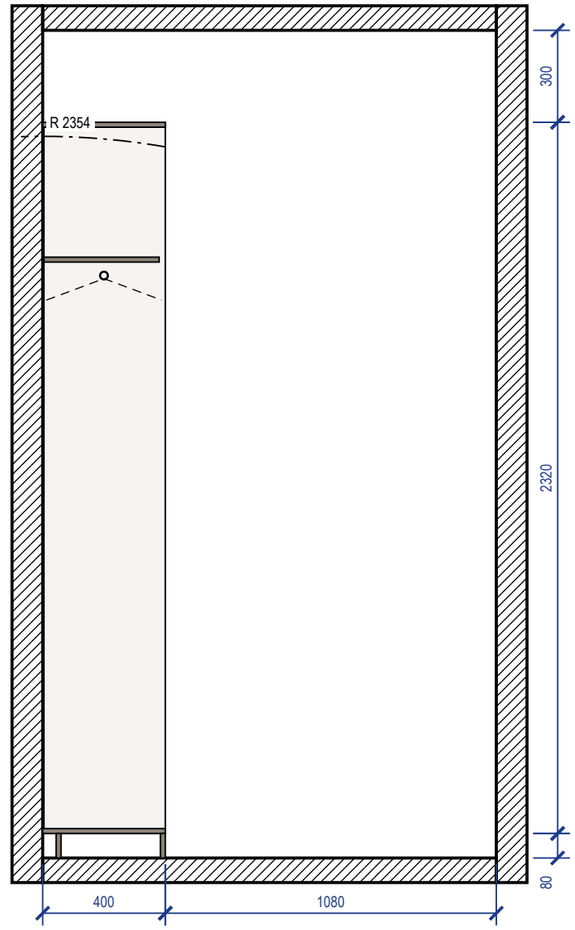


Разрез 2-2

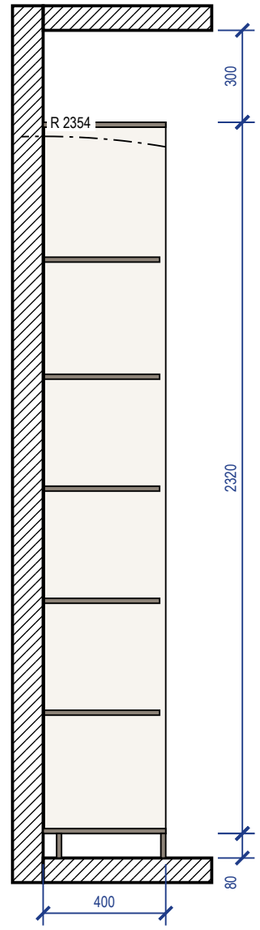

Примечания

1. Размеры — в мм по чистовой отделке; изделие 1600×400×2400 (Ш×Г×В). Перед раскроем — контрольный замер цеха после чистовой отделки стен, пола и потолка.
2. Корпус — ЛДСП 16 мм, задняя стенка ХДФ 4 мм в паз, цоколь 80 мм на регулируемых опорах; открытая система: без фасадов.
3. Кромка: скрытые торцы 0,4 мм, видимые 2 мм (ПВХ/АБС).
4. Присадка по 32-й системе — выполняет цех.
5. Зазор до потолка 300 мм.
6. Подъём корпуса: диагональ боковины без цоколя $\sqrt{(2320^2 + 400^2)} = 2354$ мм < 2700 мм до потолка — корпус собирается лёжа, поднимается поворотом и ставится на цоколь.
7. Крепление к стене от опрокидывания — уголки 2 шт. к несущему основанию (монтажная схема шкафов).
8. Проход перед изделием 1080 мм показан на разрезе 1-1.


3D орто

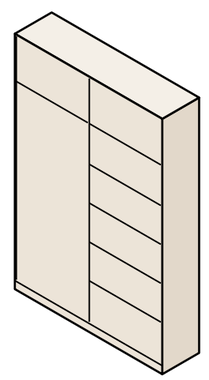


					Проект: Квартира 65 м²	**М 1:20**
	Лист	№ док.	Подпись	Дата	Система хранения М_18	Стадия / Лист / Листов
Дизайнер	Кырлан А.С.			04.11.26		П / Д_3 / 83

выпуск 04.11.2026 № 84932ed378 · стр. 75 из 83


Вид с фасадами

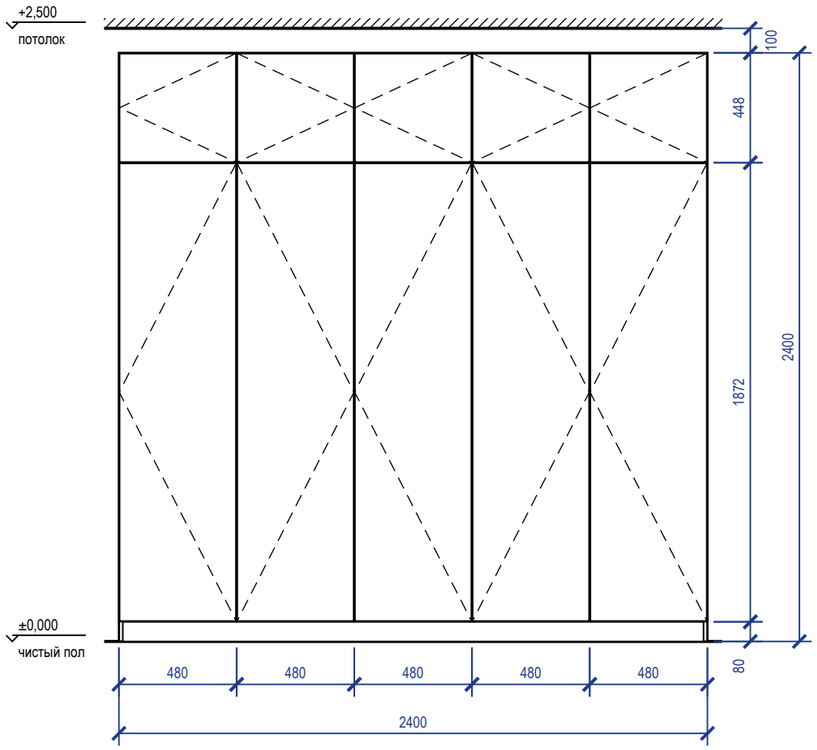


Вид без фасадов

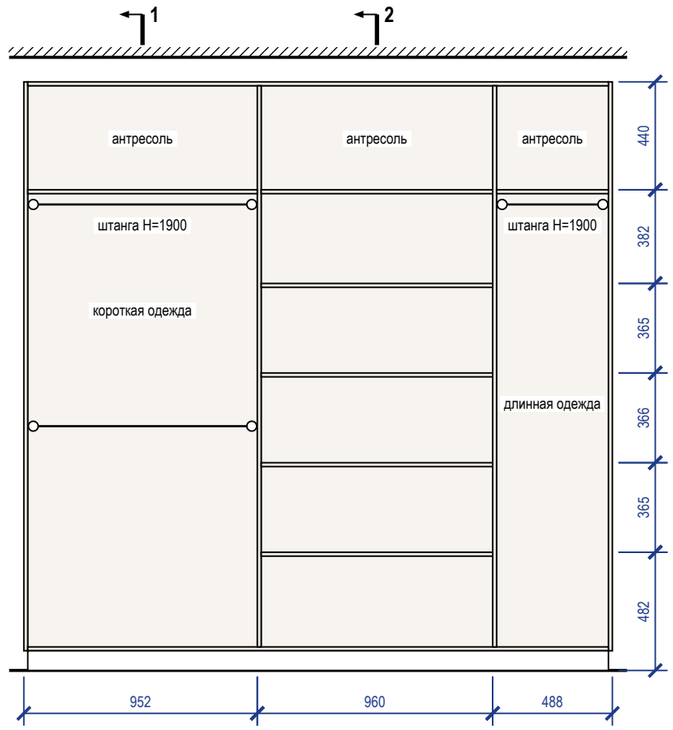

Разрез 1-1

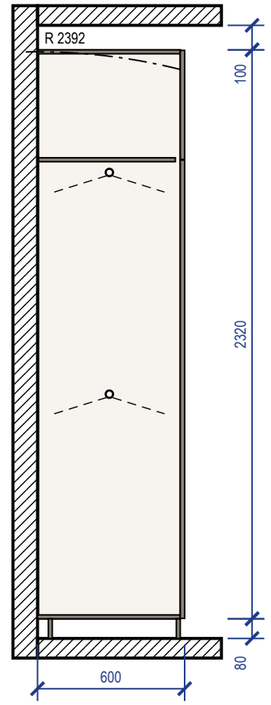


Разрез 2-2

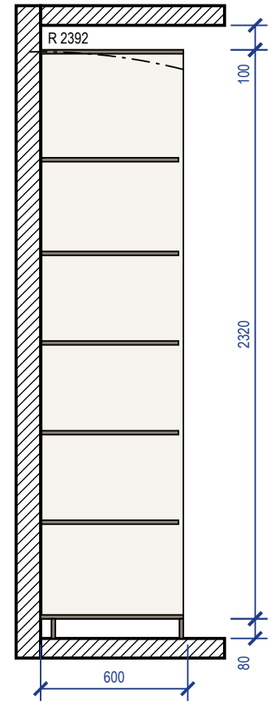

Примечания

1. Размеры — в мм по чистовой отделке; изделие 2400×600×2400 (Ш×Г×В). Перед раскроем — контрольный замер цеха после чистовой отделки стен, пола и потолка.
2. Корпус — ЛДСП 16 мм, задняя стенка ХДФ 4 мм в паз, цоколь 80 мм на регулируемых опорах; фасады накладные — МДФ 18 мм, эмаль матовая, 18 мм; цвет — по колерной карте; петли с доводчиком: фасад 1869 мм — 4 петли, фасад 445 мм — 2 петли.
3. Кромка: скрытые торцы 0,4 мм, видимые 2 мм (ПВХ/АБС).
4. Номинальные зазоры: между фасадами 3 мм, фасад — стена и фасад — потолок не менее 3 мм, фасад ящика — стойка 2 мм.
5. Присадка по 32-й системе — выполняет цех.
6. Зазор до потолка 100 мм — закрыть планкой в цвет корпуса при монтаже.
7. Подъём корпуса: диагональ боковины без цоколя $\sqrt{(2320^2 + 582^2)} = 2392$ мм < 2500 мм до потолка — корпус собирается лёжа, поднимается поворотом и ставится на цоколь.
8. Крепление к стене от опрокидывания — уголки 2 шт. к несущему основанию (монтажная схема шкафов).


3D орто

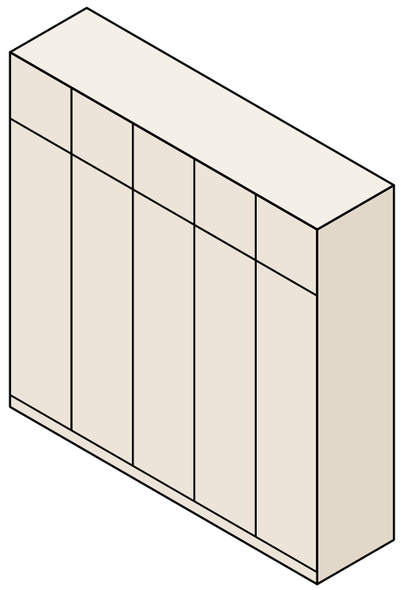


					Проект: Квартира 65 м²	М 1:25
	Лист	№ док.	Подпись	Дата	Шкаф распашной М_19	
Дизайнер	Кырлан А.С.			04.11.26		

Стадия	Лист	Листов
П	Д_4	83


Вид с фасадами

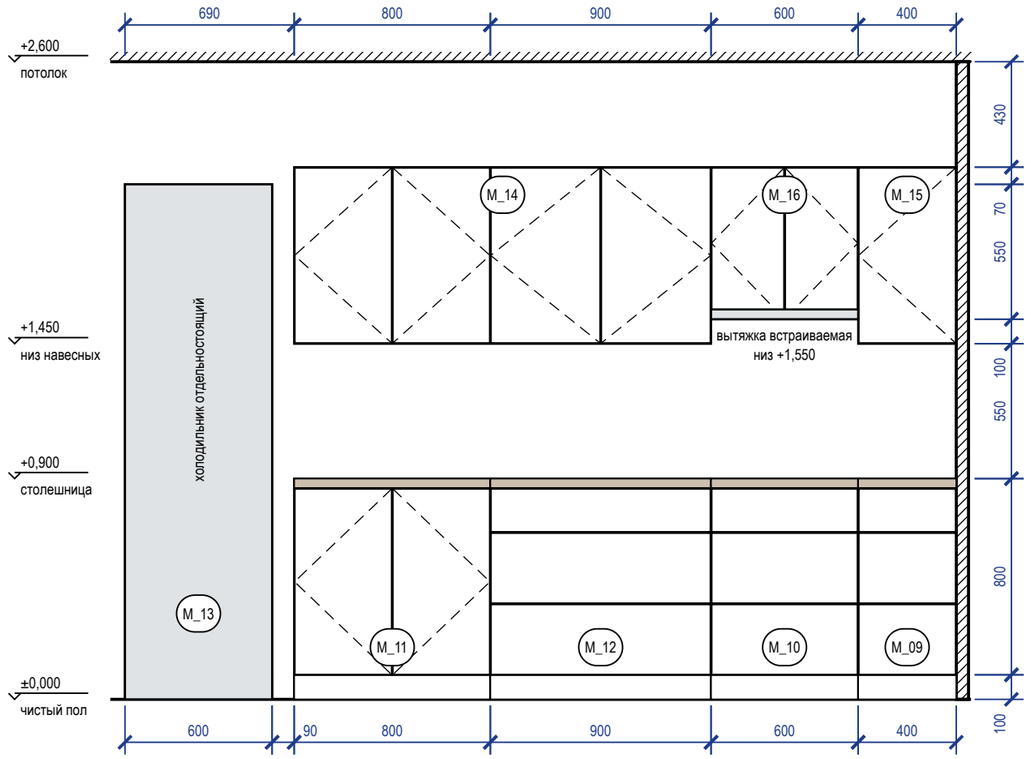


Вид без фасадов (наполнение, выводы)

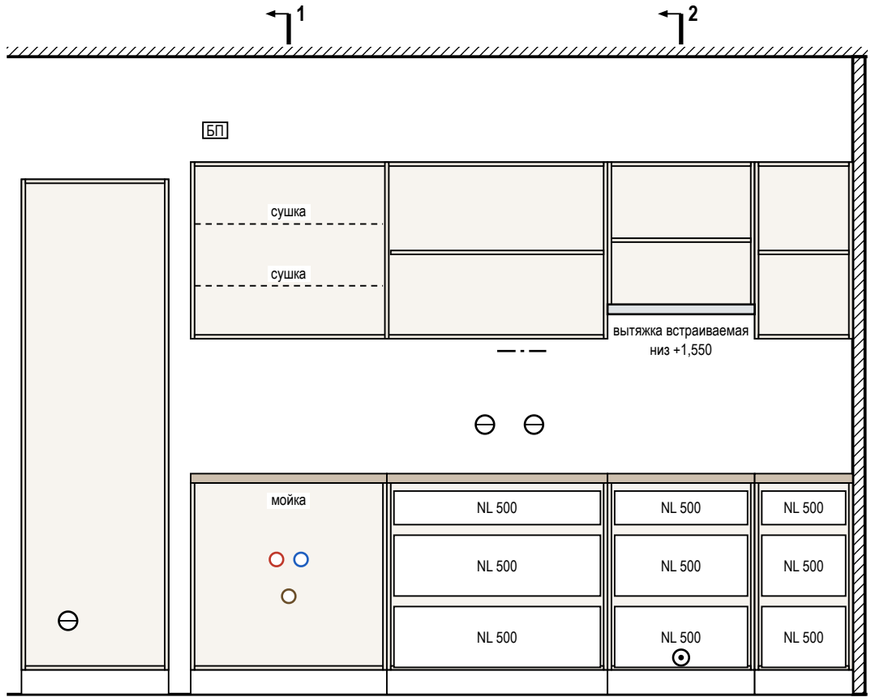


Разрез 1-1

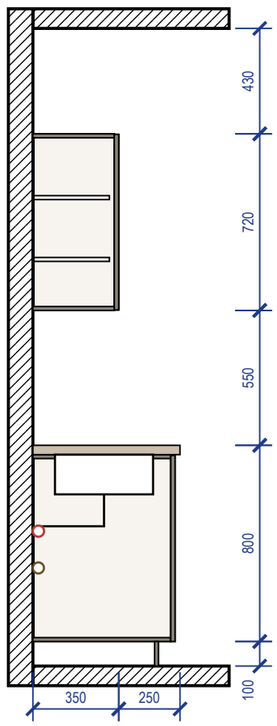

Разрез 2-2

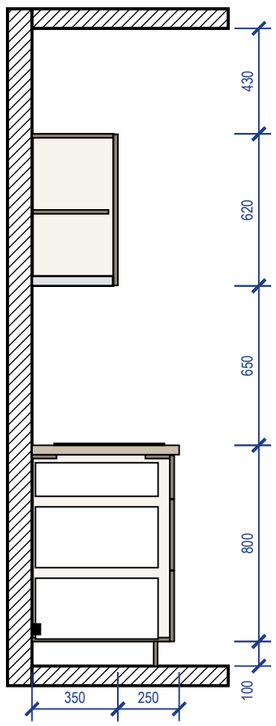

3D орто

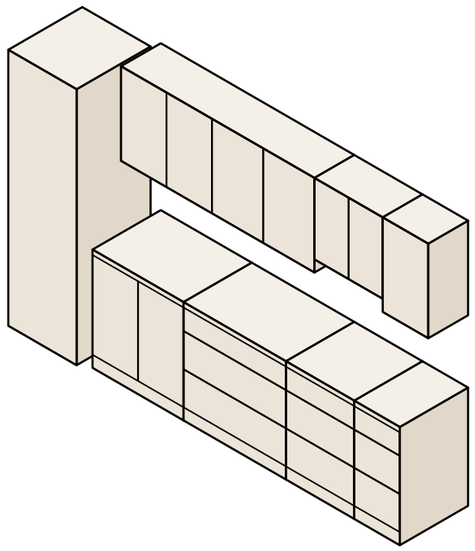

Примечания

1. Размеры — в мм по чистовой отделке, вид из помещения; марки — как на плане расстановки. Перед раскроем — контрольный замер цеха после фартука и пола.
2. Корпуса — ЛДСП 16 мм, задняя стенка ХДФ 4 мм; фасады — МДФ эмаль 18 мм, цвет по колерной карте; столешница 38 мм, свес 20 мм; цоколь 100 мм.
3. Кромка: скрытые торцы 0,4 мм, видимые 1 мм. Номинальные зазоры: между фасадами 3 мм, фасад — столешница 3 мм, фасад — стена не менее 3 мм.
4. Ящики полного выдвижения и петли — с доводчиком; присадка по 32-й системе — выполняет цех.
5. Вытяжка встраивается в дно навесного модуля M_16 над варочной: её низ на 1550 мм от пола, 650 мм над панелью (не меньше 650 мм).
6. Ниши техники — по монтажным схемам выбранных моделей: решётка в цоколе и канал за пеналом холодильника, зазор за духовым шкафом, фасад ПММ на двери машины.

					Проект: Квартира 65 м²		**М 1:25**
	Лист	№ док.	Подпись	Дата	Кухня (пом. 3). Развёртка гарнитура	Стадия	Лист	Листов
Дизайнер	Кырлан А.С.			04.11.26		П	Д_5	83

Ведомость отделки помещений (форма 1 прил. А ГОСТ 21.501-2018)

№	Наименование помещения	Потолок			Стены и перегородки			Низ стен (плинтус)			Пол		Примечание
		Вид отделки	Код цвета	S, м²	Вид отделки	Код цвета	S, м²	Вид отделки	Код цвета	L, м	Вид отделки	S, м²	
1	Гардеробная 4,20 м²	Существующий потолок, отм. +2,700; окраска, Tikkurila Anti-Reflex 2, глубокоматовая, 2 слоя, подготовка Q3	Tikkurila V503	4,20	Окраска, Tikkurila Harmony, матовая, 2 слоя, подготовка Q3	Tikkurila V503	21,37	Плинтус МДФ h=69 мм, SX165	Tikkurila V503	7,8	Инженерная доска, 1167-1101, 2100×127 мм, на клею; тип 1, отм. ЧП ±0,000	4,20	H стен 2700 (до потолка); плинтус в цвет: стены
2	Спальня 8,27 м²	ГКЛ по каркасу П113, отм. +2,600; окраска, Tikkurila, глубокоматовая	NCS S 0300-N	8,27	Окраска, Tikkurila, глубокоматовая, подготовка Q3	NCS S 1502-Y50R	27,38	Плинтус МДФ h=69 мм, SX165	NCS S 0300-N	10,3	Инженерная доска, 1167-1101, 2100×127 мм, на клею; тип 1, отм. ЧП ±0,000	8,27	H стен 2600 (до потолка)
3	Кухня-гостиная 18,91 м²	ГКЛ по каркасу П113, отм. +2,600; окраска, Tikkurila, глубокоматовая	NCS S 0300-N	18,91	Окраска, Tikkurila, полуматовая, подготовка Q3	NCS S 1002-Y50R	46,29	Плинтус МДФ h=69 мм, SX165	NCS S 0300-N	18,6	Инженерная доска, 1167-1101, 2100×127 мм, на клею; тип 1, отм. ЧП ±0,000	18,91	H стен 2600 (до потолка)
4	Прихожая 4,15 м²	ГКЛ по каркасу П113, отм. +2,600; окраска, Tikkurila, глубокоматовая	NCS S 0300-N	4,15	Окраска, Tikkurila, полуматовая, подготовка Q3	NCS S 1502-Y50R	16,60	Плинтус МДФ h=69 мм, SX165	NCS S 0300-N	6,0	Керамогранит, SG501600R, 600×1200 мм; тип 2, отм. ЧП ±0,000	4,15	H стен 2600 (до потолка)
5	Коридор 5,51 м²	ГКЛ по каркасу П113, отм. +2,600; окраска, Tikkurila, глубокоматовая	NCS S 0300-N	5,51	Окраска, Tikkurila, полуматовая, подготовка Q3	NCS S 1502-Y50R	20,60	Плинтус МДФ h=69 мм, SX165	NCS S 0300-N	7,0	Керамогранит, SG501600R, 600×1200 мм; тип 2, отм. ЧП ±0,000	5,51	H стен 2600 (до потолка)
6	Санузел 1,83 м²	ГКЛВ по каркасу П113, отм. +2,600; окраска, Tikkurila, глубокоматовая	NCS S 0300-N	1,83	Облицовка плиткой, 610010001195, 600×1200 мм, клей C2	Italon 610010001195	13,33	нет (облицовка от пола)			Керамогранит, SG501600R, 600×1200 мм; тип 3, отм. ЧП −0,015	1,83	H стен 2615 (до потолка); гидроизоляция обмазочная, 2 слоя, с заведением на стены 200 мм (по пирогу пола); тест проливом и акт скрытых работ
7	Ванная 3,85 м²	ГКЛВ по каркасу П113, отм. +2,600; окраска, Tikkurila, глубокоматовая	NCS S 0300-N	3,85	Облицовка плиткой, 610010001195, 600×1200 мм, клей C2	Italon 610010001195	19,29	нет (облицовка от пола)			Керамогранит, SG501600R, 600×1200 мм; тип 3, отм. ЧП −0,015	3,85	H стен 2615 (до потолка); тёплый пол; гидроизоляция обмазочная, 2 слоя, с заведением на стены 200 мм; над ванной — до 2000 и 300 мм за борт (по пирогу пола); тест проливом и акт скрытых работ
8	Кладовая 2,50 м²	Существующий потолок, отм. +2,700; окраска, Tikkurila, глубокоматовая	NCS S 0300-N	2,50	Окраска, Tikkurila, матовая, подготовка Q3	NCS S 0502-Y	15,65	Плинтус МДФ h=69 мм, SX165	NCS S 0300-N	5,6	Инженерная доска, 1167-1101, 2100×127 мм, на клею; тип 1, отм. ЧП ±0,000	2,50	H стен 2700 (до потолка)
9	Детская 16,02 м²	ГКЛ по каркасу П113, отм. +2,500; +2,600; окраска, Tikkurila Anti-Reflex 2, глубокоматовая, 2 слоя, подготовка Q3	Tikkurila V503	16,02	Окраска, Farrow & Ball Modern Emulsion, матовая, 2 слоя, подготовка Q3 Акцент — стена A: окраска, Farrow & Ball Modern Emulsion, матовая, 2 слоя, подготовка Q3	Farrow & Ball No. 241 Farrow & Ball No. 30	24,27 13,35	Плинтус МДФ h=69 мм, SX165	Farrow & Ball No. 241	15,9	Инженерная доска, 1167-1101, 2100×127 мм, на клею; тип 1, отм. ЧП ±0,000	16,02	H стен 2500 (до потолка); плинтус в цвет: стены
	Итого			**65,24**			**218,12**			**71,1**		**65,24**	

Примечания

1. Площади поверхностей — по чистым граням стен до отделки: стены = периметр × высоту от чистого пола помещения до низа потолка минус проёмы (облицовка плиткой — до верха облицовки); плинтус = периметр минус дверные проёмы; пол и потолок — по площади помещения. Количество плиток по раскладке. Площади помещений — с учётом всех частей помещения; откосы в площадь стен не входят.
2. Акцентные стены — отдельными строками, их площадь вычтена из основной отделки стен помещения.
3. Плинтус — длина по периметру за вычетом дверных проёмов; примыкания к наличникам и встроенной мебели — по развёрткам.
4. Формат плитки — Ш×В×Т (ширина × высота в положении укладки × толщина), мм; на полу — вдоль стен А/В × вдоль стен Б/Г.
5. Коды цвета — по веерам производителей; колеровка каждой краски одной партией, проверка выкраса при свете D65 и при лампах проекта.
6. Уровни подготовки Q1–Q4 — система Knauf, не норма ГОСТ/СП; допуски поверхностей — по СП 71.13330.2017 (действующая редакция).
7. «аналог:» — изделие задано характеристиками, марку и артикул согласовать с заказчиком до закупки.
8. Сводка площадей по материалам, м²: потолок — Tikkurila V503 Anti-Reflex 2 — 20,22; потолок — NCS S 0300-N — 45,02; стены — Tikkurila V503 Harmony — 21,37; стены — NCS S 1502-Y50R — 64,57; стены — NCS S 1002-Y50R — 46,29; стены — облицовка плиткой 600×1200 мм, Italon 610010001195 — 32,63; стены — NCS S 0502-Y — 15,65; стены — Farrow & Ball No. 241 Modern Emulsion — 24,27; стены — Farrow & Ball No. 30 Modern Emulsion 13,35.

					Проект: Квартира 65 м²
	Лист	№ док.	Подпись	Дата	Ведомость отделки помещений
Дизайнер	Кырлан А.С.			04.11.26	

Стадия	Лист	Листов
П	С1	83

Поз.	Наименование и техническая характеристика	Тип, марка, обозначение документа	Код продукции	Поставщик	Ед. изм.	Кол.	Образец	Примечание
	Лакокрасочные материалы							
1	Краска интерьерная водно-дисперсионная акриловая для стен, матовая, класс мокрого истирания 1 по EN 13300, база A; цвет по вееру Tikkurila V503 «Winter», колеровка машинная	Tikkurila Harmony		Tikkurila	л	6,3		поз. К1 колерной карты; пом. 1; S = 21,4 м² × 2 сл. × 0,12 л/м² = 5,1 л, +10 % и 0,5 л на подкраску → ≥ 6,1 л; тара 2 × 2,7 л + 1 × 0,9 л
2	Краска интерьерная водно-дисперсионная акриловая для потолков, глубокоматовая, класс мокрого истирания 2 по EN 13300, база A; цвет по вееру Tikkurila V503 «Winter», колеровка машинная	Tikkurila Anti-Reflex 2		Tikkurila	л	6,3		поз. К2 колерной карты; пом. 1, 9; S = 20,2 м² × 2 сл. × 0,12 л/м² = 4,9 л, +10 % и 0,5 л на подкраску → ≥ 5,8 л; тара 2 × 2,7 л + 1 × 0,9 л
3	Краска интерьерная водно-дисперсионная акриловая для стен, глубокоматовая, класс мокрого истирания 2 по EN 13300, база A; цвет NCS S 1502-Y50R, колеровка машинная	Tikkurila		Tikkurila	л	8,1		поз. К4 колерной карты; пом. 2; S = 27,4 м² × 2 сл. × 0,12 л/м² = 6,6 л, +10 % и 0,5 л на подкраску → ≥ 7,7 л; тара 3 × 2,7 л
4	Краска интерьерная водно-дисперсионная для потолков, глубокоматовая, класс мокрого истирания 2 по EN 13300, база A; цвет NCS S 0300-N, колеровка машинная	Tikkurila		Tikkurila	л	3,6		поз. К5 колерной карты; пом. 2, 8; S = 10,8 м² × 2 сл. × 0,12 л/м² = 2,6 л, +10 % и 0,5 л на подкраску → ≥ 3,3 л; тара 1 × 2,7 л + 1 × 0,9 л
5	Краска интерьерная водно-дисперсионная акриловая для стен, полуматовая, класс мокрого истирания 1 по EN 13300, база A; цвет NCS S 1002-Y50R, колеровка машинная	Tikkurila		Tikkurila	л	13,5		поз. К7 колерной карты; пом. 3; S = 46,3 м² × 2 сл. × 0,12 л/м² = 11,1 л, +10 % и 0,5 л на подкраску → ≥ 12,7 л; тара 1 × 9 л + 1 × 2,7 л + 2 × 0,9 л
6	Краска интерьерная водно-дисперсионная для потолков, глубокоматовая, класс мокрого истирания 1 по EN 13300, база A; цвет NCS S 0300-N, колеровка машинная	Tikkurila		Tikkurila	л	9,9		поз. К8 колерной карты; пом. 3, 4, 5, 6, 7; S = 34,3 м² × 2 сл. × 0,12 л/м² = 8,2 л, +10 % и 0,5 л на подкраску → ≥ 9,5 л; тара 1 × 9 л + 1 × 0,9 л
7	Краска интерьерная водно-дисперсионная акриловая для стен, полуматовая, класс мокрого истирания 1 по EN 13300, база A; цвет NCS S 1502-Y50R, колеровка машинная	Tikkurila		Tikkurila	л	10,8		поз. К9 колерной карты; пом. 4, 5; S = 37,2 м² × 2 сл. × 0,12 л/м² = 8,9 л, +10 % и 0,5 л на подкраску → ≥ 10,3 л; тара 1 × 9 л + 2 × 0,9 л
8	Краска интерьерная водно-дисперсионная акриловая для стен, матовая, класс мокрого истирания 2 по EN 13300, база A; цвет NCS S 0502-Y, колеровка машинная	Tikkurila		Tikkurila	л	5,4		поз. К10 колерной карты; пом. 8; S = 15,6 м² × 2 сл. × 0,12 л/м² = 3,8 л, +10 % и 0,5 л на подкраску → ≥ 4,6 л; тара 2 × 2,7 л
9	Краска интерьерная водно-дисперсионная акриловая для стен, матовая, класс мокрого истирания 1 по EN 13300, база A; цвет по вееру Farrow & Ball No. 241 «Skimming Stone», колеровка машинная	Farrow & Ball Modern Emulsion		Farrow & Ball	л	7,5		поз. К11 колерной карты; пом. 9; S = 24,3 м² × 2 сл. × 0,12 л/м² = 5,8 л, +10 % и 0,5 л на подкраску → ≥ 6,9 л; тара 1 × 5 л + 1 × 2,5 л
10	Краска интерьерная водно-дисперсионная акриловая для акцентных стен, матовая, класс мокрого истирания 1 по EN 13300, база C; цвет по вееру Farrow & Ball No. 30 «Hague Blue», колеровка машинная	Farrow & Ball Modern Emulsion		Farrow & Ball	л	5		поз. К12 колерной карты; пом. 9; S = 13,3 м² × 2 сл. × 0,12 л/м² = 3,2 л, +10 % и 0,5 л на подкраску → ≥ 4,0 л; тара 1 × 5 л
11	Краска для МДФ и дерева в цвет Tikkurila V503 «Winter» — окраска плинтуса; блеск не ниже блеска стен	марка не задана			л	0,5		поз. К3; пом. 1; L = 7,8 м, S = 0,7 м² × 2 сл. × 0,12 л/м² + 10 %; продукт подобрать в веере Tikkurila
12	Акрил, полуматовая в цвет NCS S 0300-N — окраска плинтуса	аналог по характеристикам			л	1,1		поз. К6; пом. 2, 3, 4, 5, 8; L = 47,4 м, S = 4,0 м² × 2 сл. × 0,12 л/м² + 10 %; продукт подобрать в веере NCS
13	Краска для МДФ и дерева в цвет Farrow & Ball No. 241 «Skimming Stone» — окраска плинтуса; блеск не ниже блеска стен	марка не задана			л	0,5		поз. К13; пом. 9; L = 15,9 м, S = 1,3 м² × 2 сл. × 0,12 л/м² + 10 %; продукт подобрать в веере Farrow & Ball
14	Грунтовка акриловая под окраску стен и потолков — из системы производителя краски	по системе краски			м²	251		площадь окраски стен, акцентов и потолков; 1 слой перед окраской; расход — по ТУ грунтовки

					Проект: Квартира 65 м²	
	Лист	№ док.	Подпись	Дата	Спецификация отделочных материалов	Стадия / Лист / Листов
Дизайнер	Кырлан А.С.			04.11.26		П / С2 / 83

Поз.	Наименование и техническая характеристика	Тип, марка, обозначение документа	Код продукции	Поставщик	Ед. изм.	Кол.	Образец	Примечание
	Плитка и керамогранит							
15	SG501600R, 600×1200 мм, противоскольжение R10	SG501600R		Kerama Marazzi	м²	23,04		шов 2 мм; Санузел, пол; Ванная, пол; Прихожая, пол; Коридор, пол; по раскладке 28 шт (S = 15,34 м²), с запасом 32 шт
16	610010001195, 1200×600 мм	610010001195		Italon	м²	56,16		шов 2 мм; Санузел, стены А–Г; Ванная, стены А–Г; по раскладке 70 шт (S = 32,62 м²), с запасом 78 шт
	Напольные покрытия							
17	1167-1101, рабочий слой 4 мм, эмиссия E1, укладка на клей	1167-1101		Coswick	м²	21,7		пом. 1, 9; S = 20,22 м² + 7 % (прямая укладка); к заказу — кратно упаковке
18	1167-1101, класс 33, рабочий слой 4 мм, эмиссия E1, укладка на клей	1167-1101		Coswick	м²	31,8		пом. 2, 3, 8; S = 29,68 м² + 7 % (прямая укладка); к заказу — кратно упаковке
19	Клей для паркета и инженерной доски, эластичный (СМП / полиуретановый)	по рекомендации производителя доски			м²	50		площадь приклейки; расход и шпатель — по ТУ клея
	Погонажные изделия							
20	SX165, h = 69 мм, крепление к стене, окраска в цвет Tikkurila V503	SX165		Orac Decor	м	9		пом. 1; L = 7,8 м (периметр без дверных проёмов) + 10 % на подрезку; в штуках — по длине планки
21	SX165, h = 69 мм, крепление к стене, окраска в цвет NCS S 0300-N	SX165		Orac Decor	м	53		пом. 2, 3, 4, 5, 8; L = 47,4 м (периметр без дверных проёмов) + 10 % на подрезку; в штуках — по длине планки
22	SX165, h = 69 мм, крепление к стене, окраска в цвет Farrow & Ball No. 241	SX165		Orac Decor	м	18		пом. 9; L = 15,9 м (периметр без дверных проёмов) + 10 % на подрезку; в штуках — по длине планки
	Смеси и материалы для облицовки							
23	Затирка для швов плитки	аналог по характеристикам			кг	3,7		по раскладке (a+b)/(a·b) × шов × t × 1,6 + 10 %
24	Клей плиточный C2 S1 по EN 12004, слой 5 мм	аналог по характеристикам			кг	45		2 меш. по 25 кг; 1,5 кг/м² на 1 мм слоя + 10 %
25	Клей плиточный C2 по EN 12004, слой 5 мм	аналог по характеристикам			кг	339		14 меш. по 25 кг; 1,5 кг/м² на 1 мм слоя + 10 %
26	Гидроизоляция обмазочная мокрых зон: пол, стены по периметру, зоны замачивания; 2 слоя с армирующей лентой в углах	аналог по характеристикам			м²	14,8		площадь по листу раскладки плитки + 10 %; расход смеси — по ТУ
27	Лента демпферная по периметру пола из плитки	аналог по характеристикам			м	27		периметр без дверных проёмов + 10 %

Примечания

1. Количества — из геометрии проекта: площади поверхностей по чистым граням стен до отделки (те же, что в ведомости отделки и колерной карте), плитка, клей и затирка — по раскладке плиточника; в графе «Кол.» — к заказу, с запасом.
2. Краска: расход 0,12 л/м² на слой в 2 слоя, если по ТУ не задан иной; запас 10 % и 0,5 л на подкраску каждого кода. Один код — одна партия, колеровка машинная в колеровочном центре бренда; в заказ — только после утверждения выкраса (колерная карта). Фасовка — по каталогу бренда на дату выпуска; к заказу — не меньше расчётного объёма.
3. «Аналог по характеристикам» — допускается изделие другого производителя с характеристиками не ниже указанных, по согласованию с автором проекта.
4. Графы «Код продукции» и «Масса 1 ед.» не заполнены: коды по классификатору продукции не присвоены, масса единицы до 25 кг (ГОСТ 21.110-2013).
5. Грунтовка и клей для доски указаны площадью обработки; объём — по ТУ выбранного продукта.

					Проект: Квартира 65 м²
	Лист	№ док.	Подпись	Дата	Спецификация отделочных материалов
Дизайнер	Кырлан А.С.			04.11.26	

Стадия	Лист	Листов
П	С3	83

Список покупок: материалы для магазина

№	Что купить	Артикул или характеристика	Нужно с запасом	Брать в магазине	Фасовка	Уточнить в магазине	Помещения	Кто покупает
Покрытия полов и облицовка								
1	Инженерная доска (дуб натуральный, рабочий слой 4 мм, эмиссия E1, прямая укладка)	1167-1101	53,72 м²	53,8 м²		уточнить в магазине: м² в упаковке	1, 2, 3, 8, 9	по проекту
2	Клей для паркетной и инженерной доски (эластичный, по ТУ изготовителя доски)	на выбор бригады по проекту	50,21 м²			уточнить в магазине: расход и фасовку — по выбранному продукту		бригада
3	Керамогранит 600×1200 мм SG501600R	SG501600R	31 шт	32 шт		уточнить в магазине: штук в коробке	4, 5, 6, 7	по проекту
4	Керамогранит 1200×600 мм 610010001195	610010001195	77 шт	78 шт		уточнить в магазине: штук в коробке	6, 7	по проекту
Сухие смеси и гидроизоляция								
5	Клей плиточный цементный класса C2 S1 (ГОСТ Р 56387-2018)	на выбор бригады по проекту	44,22 кг	2 меш.	мешок 25 кг			по проекту
6	Клей плиточный цементный класса C2 (ГОСТ Р 56387-2018)	на выбор бригады по проекту	338,14 кг	14 меш.	мешок 25 кг			по проекту
7	Затирка цементная класса класс не задан, цвет — по колерной карте	на выбор бригады по проекту	3,67 кг	2 упак.	упак. 2 кг			по проекту
8	Гидроизоляция обмазочная полимерная, 2 слоя, лента в углах, манжеты на выводах	на выбор бригады по проекту	8,94 м²			уточнить в магазине: расход и фасовку — по выбранному продукту	6, 7	бригада
9	Лента демпферная по периметру пола из плитки	на выбор бригады по проекту	27,02 м	28 м		уточнить в магазине: фасовку		бригада
10	Смесь цементно-песчаная для стяжки М200 (50 мм, 33 мм)	на выбор бригады по проекту	3,37 м³			уточнить в магазине: расход и фасовку — по выбранному продукту		бригада
11	Смесь штукатурная гипсовая для машинного и ручного нанесения по маякам, слой до 10 мм	на выбор бригады по проекту	64,89 м²			уточнить в магазине: расход и фасовку — по выбранному продукту	1, 9	бригада
Перегородки и облицовки из ГКЛВ								
12	Лист ГКЛ 12,5 мм, 2500 × 1200 мм: обшивка перегородок и облицовок, 2 слоя на сторону	на выбор бригады по проекту	20,77 м²	7 лист.	лист 3,00 м²			бригада
13	Профиль направляющий ПН 100: по потолку и полу, перемычки над проёмами	на выбор бригады по проекту	3,85 м	2 шт	хлыст 3 м			бригада
14	Профиль стоечный ПС 100: стойки через шаг каркаса и короткие над проёмами	на выбор бригады по проекту	11,88 м	4 шт	хлыст 3 м			бригада
15	Плита минераловатная звукопоглощающая в полость каркаса, толщина по глубине профиля 100 мм	на выбор бригады по проекту	5,19 м²			уточнить в магазине: расход и фасовку — по выбранному продукту		бригада
16	Лента уплотнительная самоклеящаяся под профили по потолку, полу и у примыканий к стенам	на выбор бригады по проекту	3,85 м	4 м		уточнить в магазине: фасовку		бригада
17	Саморезы для ГКЛ по металлу (по слоям обшивки), дюбели для направляющих — по ТУ изготовителя системы	на выбор бригады по проекту	18,88 м²			уточнить в магазине: расход и фасовку — по выбранному продукту		бригада
Слаботочные сети								
18	Кабель домофона — тип по системе поставщика	на выбор бригады по проекту	3,1 м	4 м		уточнить в магазине: длину бухты		бригада
19	Кабель коаксиальный RG-6 (75 Ом) к розеткам ТВ	на выбор бригады по проекту	30,2 м	31 м		уточнить в магазине: длину бухты		бригада
20	Кабель U/UTP кат. 5e (LAN, Wi-Fi и камеры по PoE)	на выбор бригады по проекту	42,7 м	43 м		уточнить в магазине: длину бухты		бригада
21	Кабель U/UTP кат. 6 (LAN, Wi-Fi и камеры по PoE)	на выбор бригады по проекту	14,2 м	15 м		уточнить в магазине: длину бухты		бригада
22	Гофротруба Ø20 для слаботочных линий, отдельно от силовых	на выбор бригады по проекту	81,2 м	82 м		уточнить в магазине: длину бухты		бригада

					Проект: Квартира 65 м²
	Лист	№ док.	Подпись	Дата	
Дизайнер	Кырлан А.С.			04.11.26	Список покупок

Стадия	Лист	Листов
П	С4	83

Список покупок: материалы для магазина (продолжение)


№	Что купить	Артикул или характеристика	Нужно с запасом	Брать в магазине	Фасовка	Уточнить в магазине	Помещения	Кто покупает
23	Розетка компьютерная RJ45, кат. 6, с рамкой и подрозетником	на выбор бригады по проекту	4 шт	4 шт	шт			бригада
24	Розетка телевизионная (коаксиальная) с рамкой и подрозетником	на выбор бригады по проекту	2 шт	2 шт	шт			бригада
25	Трубка или монитор домофона (поставка домофонной организации)	на выбор бригады по проекту	1 шт	1 шт	шт			по проекту
26	Щит слаботочный ЩС: корпус, DIN-рейка, розетки 220 В	на выбор бригады по проекту	1 шт	1 шт	шт			бригада
27	Патч-панель, портов не менее 4	на выбор бригады по проекту	1 шт	1 шт	шт			бригада
Лакокрасочные материалы								
28	Краска интерьерная акриловая, матовая, класс истирания 1	Tikkurila Harmony V503 «Winter»	5,64 л	3 банк.	банка 2,7 л		1	по проекту
29	Краска интерьерная акриловая, глубокоматовая, класс истирания 2	Tikkurila Anti-Reflex 2 V503 «Winter»	5,34 л	2 банк.	банка 2,7 л		1, 9	по проекту
30	Краска интерьерная акриловая, глубокоматовая, класс истирания 2	Tikkurila S 1502-Y50R	7,23 л	3 банк.	банка 2,7 л		2	по проекту
31	Краска интерьерная водно-дисперсионная, глубокоматовая, класс истирания 2	Tikkurila S 0300-N	11,88 л	5 банк.	банка 2,7 л		2, 3, 4, 5, 6, 7, 8	по проекту
32	Краска интерьерная акриловая, полуматовая, класс истирания 1	Tikkurila S 1002-Y50R	12,22 л	5 банк.	банка 2,7 л		3	по проекту
33	Краска интерьерная акриловая, полуматовая, класс истирания 1	Tikkurila S 1502-Y50R	9,82 л	4 банк.	банка 2,7 л		4, 5	по проекту
34	Краска интерьерная акриловая, матовая, класс истирания 2	Tikkurila S 0502-Y	4,14 л	2 банк.	банка 2,7 л		8	по проекту
35	Краска интерьерная акриловая, матовая, класс истирания 1	Farrow & Ball Modern Emulsion No. 30 «Hague Blue»	3,52 л	2 банк.	банка 2,5 л		9	по проекту
36	Краска интерьерная акриловая, матовая, класс истирания 1	Farrow & Ball Modern Emulsion No. 241 «Skimming Stone»	6,4 л	3 банк.	банка 2,5 л		9	по проекту
37	Шпаклёвка финишная полимерная под окраску (стены и потолки, Q3)	на выбор бригады по проекту	275,83 м²			уточнить в магазине: расход и фасовку — по выбранному продукту		бригада
38	Грунтовка акриловая глубокого проникновения, 2 слоя	на выбор бригады по проекту	311,71 м²			уточнить в магазине: расход и фасовку — по выбранному продукту		бригада
Погонажные изделия и потолки								
39	Плинтус напольный МДФ под покраску, h=69 мм, крепление к стене	SX165	78,16 м.п.	33 шт	хлыст 2,4 м		1, 2, 3, 4, 5, 8, 9	по проекту
40	Потолок подвесной ГКЛ/ГКЛВ по каркасу Knauf П113: листы, профили, подвесы, лента, шпаклёвка швов	Knauf П113	58,54 м²			уточнить в магазине: расход и фасовку — по выбранному продукту		по проекту

Примечания


1. «Нужно с запасом» — расход по чертежам и раскладке плюс запас на подрезку и подкраску; «Брать в магазине» — то же количество в единицах, которыми продают (банки, мешки, упаковки, листы, штуки, литры).
2. «Уточнить в магазине» — фасовки этого товара в проекте нет: спросите у продавца, сколько в упаковке, и возьмите целое число упаковок не меньше «Нужно с запасом».
3. Плитку, доску и краску одного цвета берите одной партией (один калибр и тон на помещение) и сохраните чек и номер партии до конца ремонта.
4. «По характеристике» — артикул не выбран: подойдёт любой товар с этими свойствами, согласуйте его с дизайнером до покупки. «Бригада» материал выбирает и закупает бригада по своей технологии.
5. Помещения: 1 — Гардеробная; 2 — Спальня; 3 — Кухня-гостиная; 4 — Прихожая; 5 — Коридор; 6 — Санузел; 7 — Ванная; 8 — Кладовая; 9 — Детская; «—» — материал для нескольких помещений, расход по месту.

					Проект: Квартира 65 м²	
	Лист	№ док.	Подпись	Дата	Список покупок (окончание)	Стадия / Лист / Листов
Дизайнер	Кырлан А.С.			04.11.26		П / С5 / 83


1 **Порог 15 мм: мокрая зона — смежное помещение (М 1:5)**
Применение: двери Д-5, Д-4

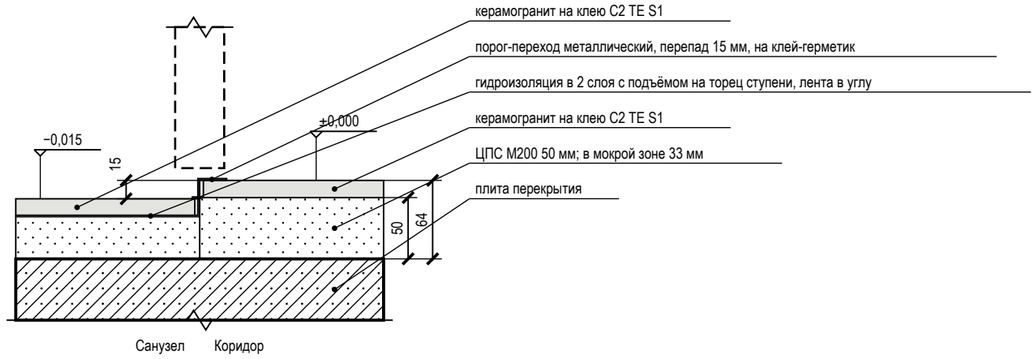


2 **Дверь скрытого монтажа в плоскости стены, плинтус (М 1:5)**
Применение: двери Д-3, Д-2, Д-5, Д-4

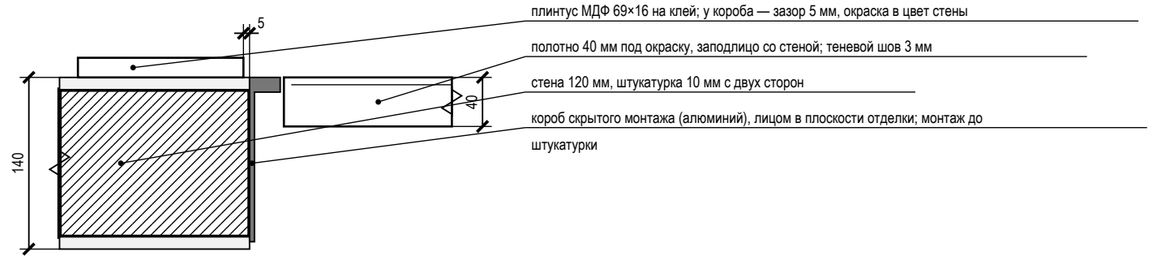


3 **Короб стояков К1-1 с люком и звукоизоляцией (М 1:20)**
Применение: пом. 6

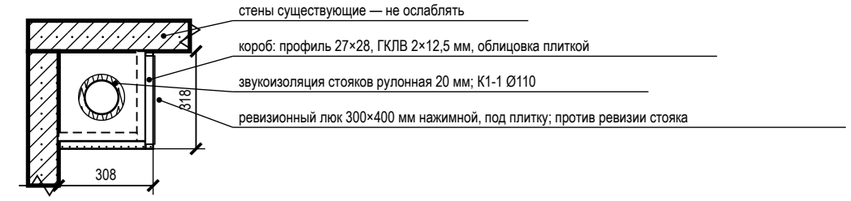


4 **Гидроизоляция санузла: заход на стены 200 мм, примыкание ванны (М 1:20)**
Применение: пом. 6, 7

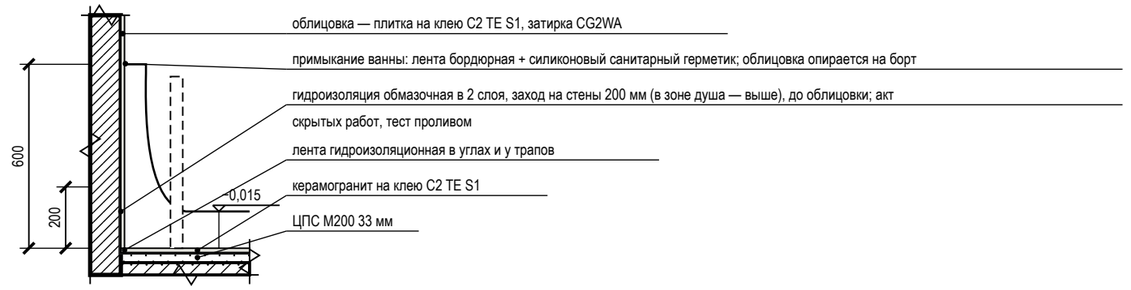

5 **Плинтус МДФ 69×16 мм у окрашенной стены по доске (ламинату) (М 1:10)**
Применение: пом. 1, 2, 3, 8, 9

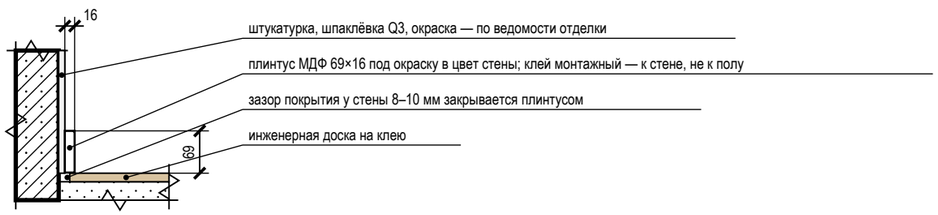

6 **Плинтус МДФ 69×16 мм у окрашенной стены по керамограниту (плитке) (М 1:10)**
Применение: пом. 4, 5

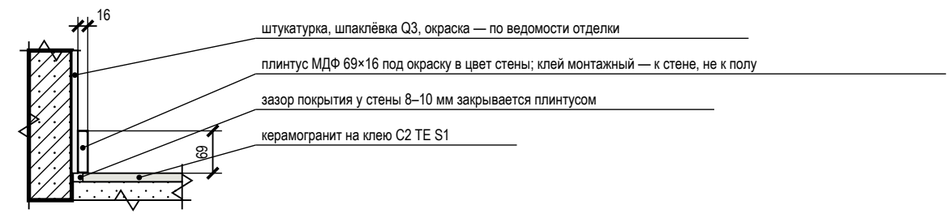

Условные обозначения

- железобетон (плита, стены) — условно: конструкция не установлена
- кладка, перегородка — условно: конструкция не установлена
- стяжка, раствор
- гипсокартон ГКЛВ
- звукоизоляция, эластичный заполнитель
- плитка, керамогранит на клею
- инженерная доска (покрытие пола)
- металлический профиль (порог, Т-профиль, короб двери)
- гидроизоляция (обмазочная, лента)

Примечания

1. Узлы — типовые решения проекта для мест, отмеченных выносками на листе схемы расположения развёрток и узлов; размеры — в мм, отметки — в м от ±0,000.
2. Узлы с гидроизоляцией, закладными и коробами скрытого монтажа принимаются по актам скрытых работ до закрытия отделкой; гидроизоляция — после теста проливом (24 ч).
3. Марки изделий (порог, Т-профиль, короб скрытой двери, люк) — по спецификациям; замена — на аналог с теми же габаритами по согласованию с автором проекта.
4. Материал плиты перекрытия и стен в узлах показан условно (железобетон, кладка): конструкция дома не установлена — крепёж, анкеры и толщины слоёв уточняются после обследования (до него — по допущениям общих указаний).

	Лист	№ док.	Подпись	Дата
Дизайнер	Кырлан А.С.			04.11.26

Проект: Квартира 65 м²

Узлы	Стадия	Лист	Листов
	П	С6	83

выпуск 04.11.2026 № 84932ed378 · стр. 83 из 83