
L

LINEA

ДИЗАЙН-ПРОЕКТ ИНТЕРЬЕРА

Квартира с кабинетом

современный модерн

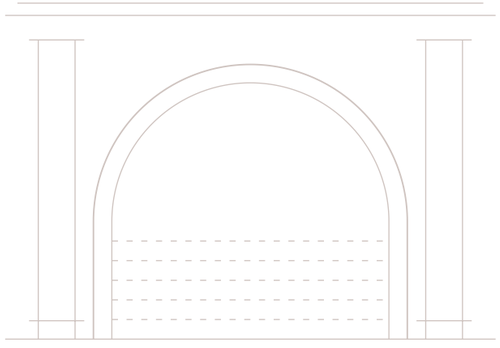


ПАЛИТРА ОТДЕЛКИ

F&B No. 15	V503	F&B No. 34	NCS S 2010-Y30	NCS S 5020-G50
49 %	41 %	9 %	текстиль, декор	текстиль, декор

АВТОР ПРОЕКТА

Кырлан Александр Сергеевич

Ноябрь 2026

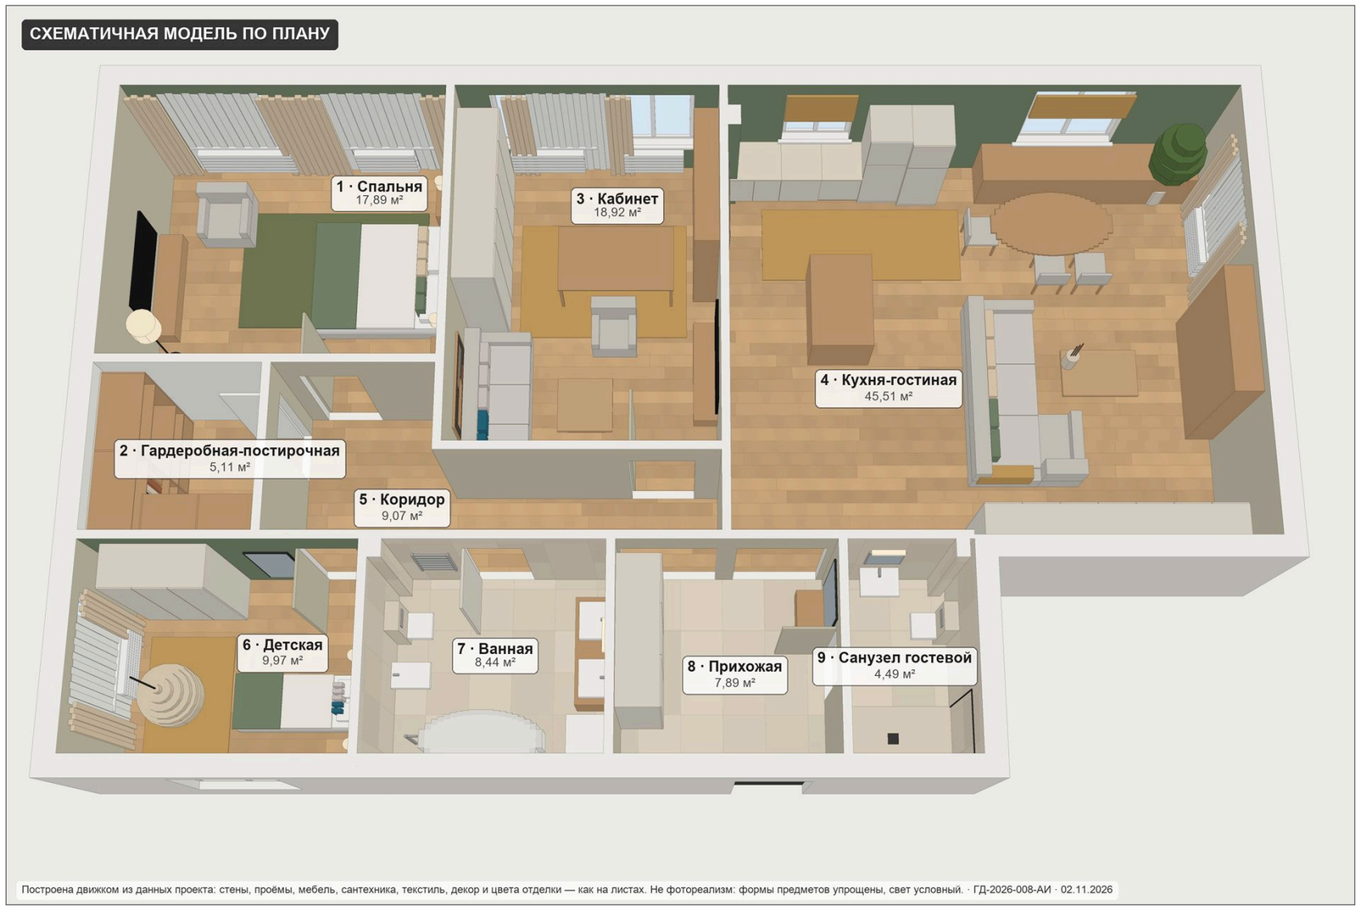


Квартира сверху · схематичная модель по плану

ОБЩАЯ ПЛОЩАДЬ	ПОМЕЩЕНИЙ	СТАДИЯ	ШИФР	ОСНОВА
127,29 м²	9, из них жилых 4	Проект · предварительно	ГД-2026-008-АИ	план заказчика, без обмера

Как оставить правку: кнопка «Правка к этому листу» в правом верхнем углу любого листа · все листы проекта: дизайн-студия-квартир.рф/review.html?p=gost-modern4k

выпуск 04.11.2026 № 627e1ac6ce · стр. 1 из 127

СХЕМАТИЧНАЯ МОДЕЛЬ ПО ПЛАНУ

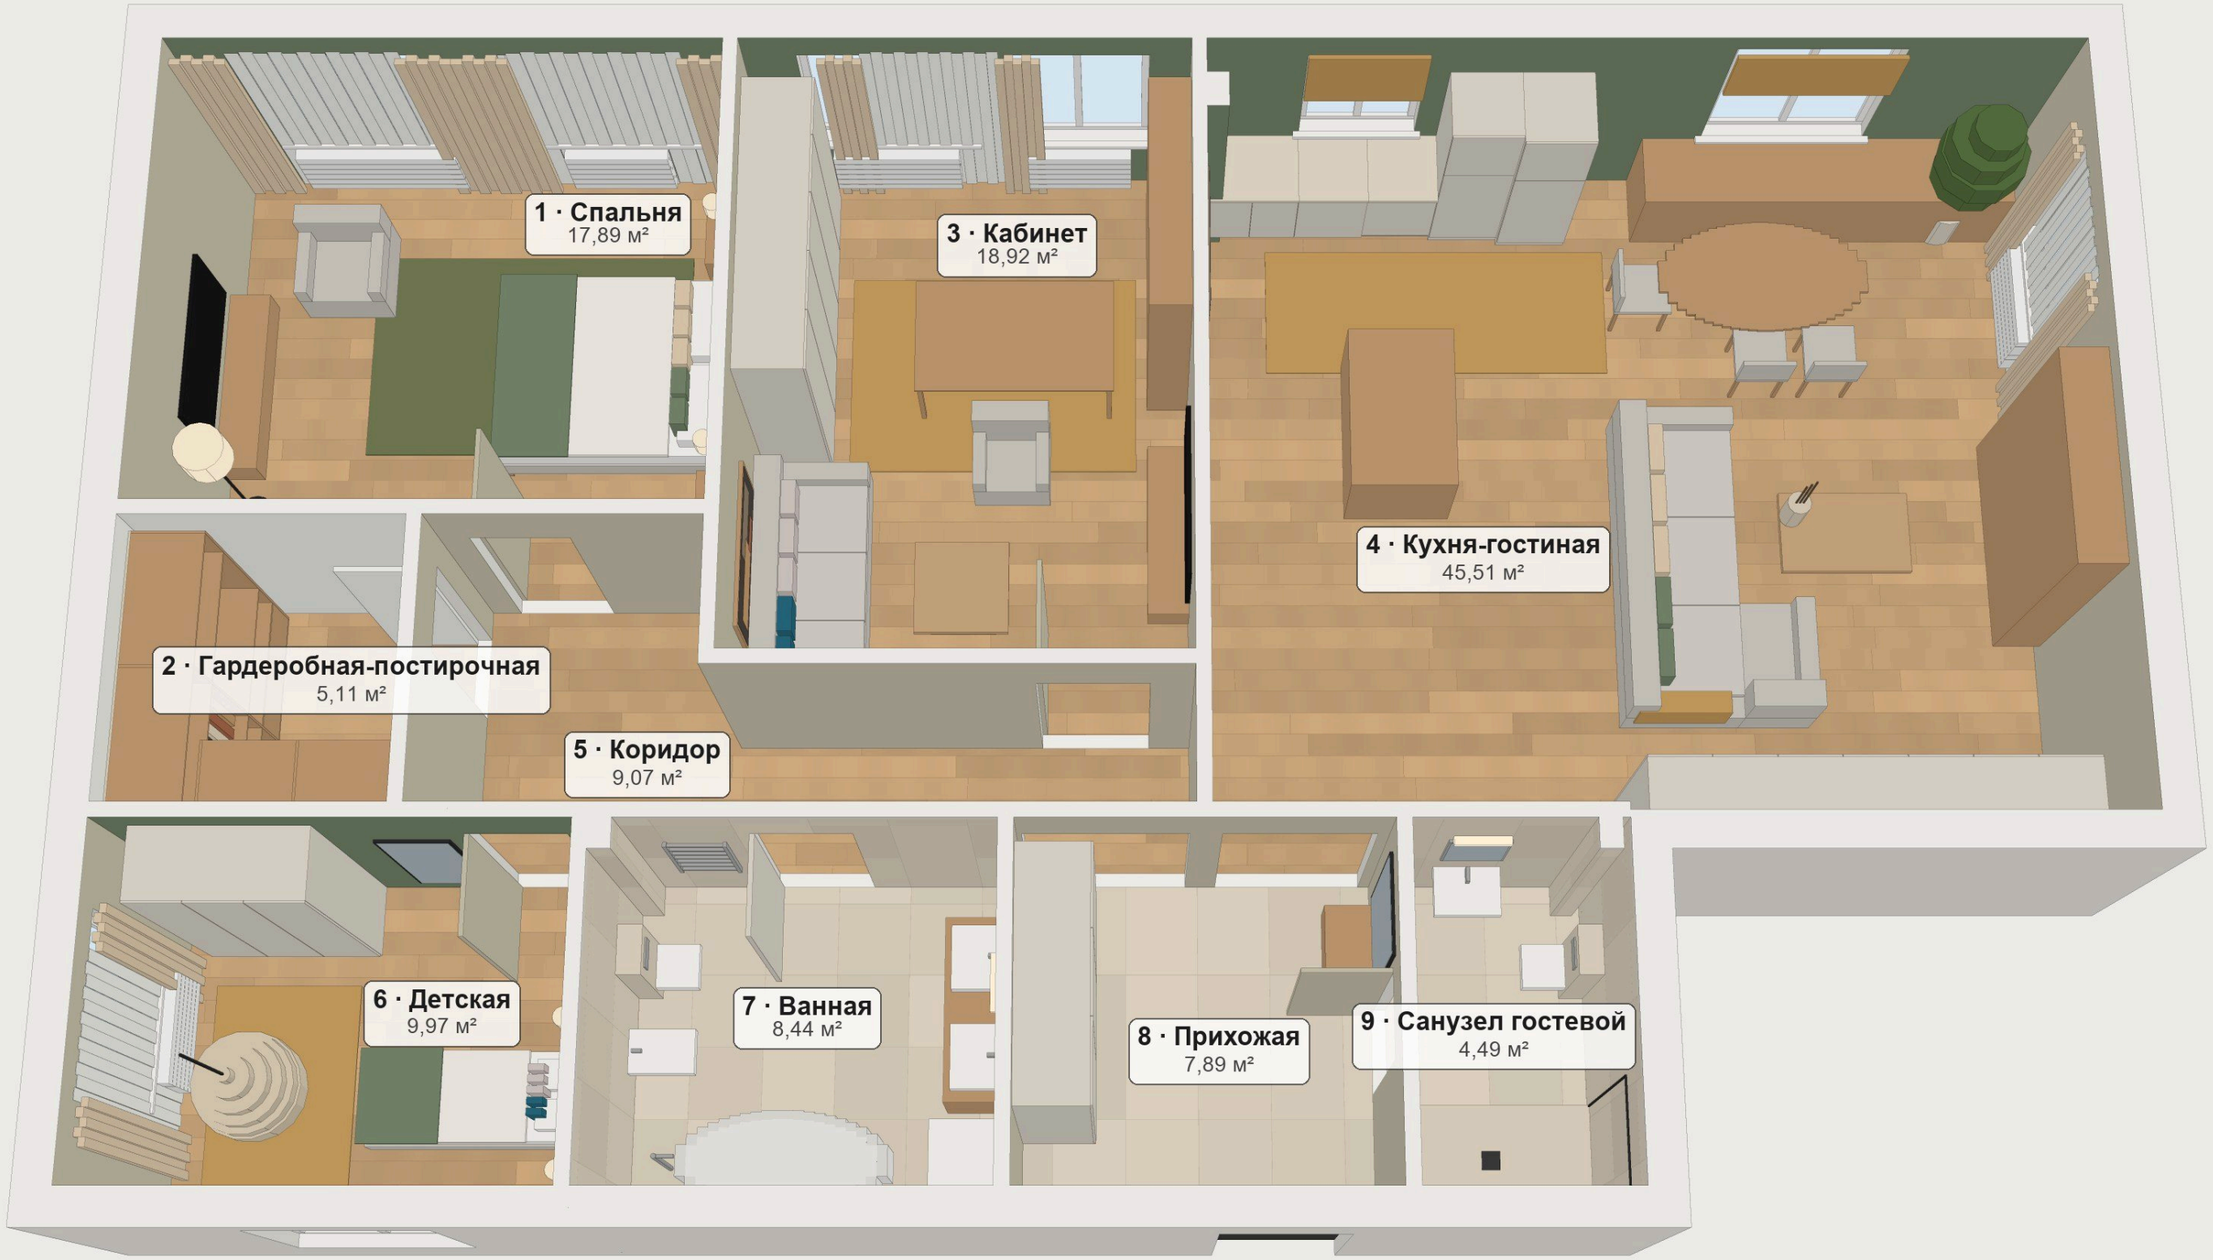

Построена движком из данных проекта: стены, проёмы, мебель, сантехника, текстиль, декор и цвета отделки — как на листах. Не фотореализм: формы предметов упрощены, свет условный. · ГД-2026-008-АИ · 02.11.2026

					Проект: Квартира с кабинетом
	Лист	№ док.	Подпись	Дата	
Дизайнер	Кырлан А.С.			04.11.26	Визуализация. Вид сверху

Стадия	Лист	Листов
П	2	127

выпуск 04.11.2026 № 627e1ac6ce · стр. 2 из 127

Объект

Квартира с кабинетом: 127,29 м², помещений 9, из них жилых 4.

Стиль: модерн (ар-нуво) 60 %, современный (контемпорари) 40 %. Стадия: предварительный альбом без обмера, планировка по плану заказчика.

Открытых вопросов 13, конфликтов разделов 0; изменений утверждено 9, ждут подписи 0.

Розетки и выводы

41 розетка (рамок 34), 7 выводов кабеля под технику и свет, 14 групп щита — всё с высотами от чистого пола: листы 63, 64, 65.

Что решено (подписано вами)

ИЗ-1 — M_30 — фасад МДФ 10 мм, эмаль матовая, профиль латунь матовая, зеркальные арочные вставки (поле 100 мм), как на кадре.

ИЗ-2 — Проём Д-6 сдвинут вдоль стены А от угла Б: привязка 2300 → 1200 (x 4900…5700), петли у x 4900, открывание внутрь, в сторону стены Г (там полотенцесушитель С_06 на стене А…

ИЗ-3 — M_05 переставлено в угол у окна 1 (x 600…1350, y 600…1350), столик M_04 свободен.

ИЗ-4 — Мебель кабинета — M_08, M_09, M_10, M_11, M_12, M_13, ОБ_02, мебель прихожей — M_30 (шкаф-купе), M_31 (банкетка).

ИЗ-5 — M_24 — каркас из оцинкованного профиля на стене Б с облицовкой панелями МДФ 19 мм, эмаль.

ИЗ-6 — РО-5 — на свободном участке наружной стены А между колонной M_14 и банкеткой M_20: привязка 3350, 500×600, низ +120 (x 11750…12250).

ИЗ-7 — РО-6 — низкий панельный прибор 1400×200 по ширине окна 2 (привязка 4400, низ +120, верх +320).

ИЗ-8 — Островная потолочная вытяжка 900 мм над M_19 в режиме рециркуляции (угольный фильтр), низ +1550.

ИЗ-9 — Биокамин в ТВ-стене M_24 остаётся, ниша 900×400, низ +350, облицовка негорючая (сталь 2 мм / камень), зазоры 50 мм до панелей.

Что ждёт вашего ответа

К-1 — Размеры квартиры сняты с растрового плана заказчика с частичными размерами (рисунок не в масштабе): помещения выровнены по подписанным размерам мебели и проходов.

К-2 — Высота потолка на плане заказчика не указана, принята 2700 мм.

К-4 — Разрешённая мощность квартиры по ТУ неизвестна, принята 15 кВт.

К-5 — Перепланировка (гардеробная-постирочная при спальне, Г-образный коридор, широкий проём прихожая гостиная, гостевой санузел у прихожей): несущие…

К-6 — Климатический подрайон (СП 131.13330) не задан: принят не северный — жилые комнаты и кухня под потолком от 2,5 м (СП 54, п. 5.12).

К-7 — Проёмы скрытых дверей Д-2 … Д-7 по плану заказчика высотой 2100 мм, полотно расчётное 2000 мм (ряд UNION FILO-60 Piatto).

К-8 — Входная дверь Д-1 (проём 1000 × 2100 мм по плану заказчика): стальной дверной блок не выбран — размер блока и монтажный зазор (ГОСТ 31173-2016) из проёма не выводятся, на…

К-10 — Душ С_07 с трапом (пом. 9, санузел гостевой, по плану заказчика — «душ с трапом и стеклянной перегородкой»): в стяжке 35 мм с облицовкой 14 мм трап не встаёт — монтажная высота…

К-11 — Ванна С_01 отдельностоящая со смесителем напольным (пом. 7, ванная, по заказчику): подвод ХВ и ГВ к стойке и выпуск Ø50 идут из пола, а стяжка ванной 35 мм их не укрывает — под…

К-12 — Проверяющий («Пров.») и нормоконтролёр («Н. контр.») комплекта не назначены: графы штампа пусты на всех листах, данные проекта и данные проекта не заданы.

К-17 — Циркуляция ГВС в данных не задана — циркуляционного трубопровода на схеме нет.

К-19 — Кухня-гостиная (пом. 4, 45,5 м², два окна): мощность приборов не подтверждена расчётом — РО-5 500×600 (вынесен из модулей, ИЗ-6) и низкий РО-6 1400×200 под банкеткой-экраном…

К-20 — ТВ-стена M_24: низ ниши ТВ (+900) — в 150 мм над верхом ниши биокамина (+750).

					Проект: Квартира с кабинетом			
	Лист	№ док.	Подпись	Дата	Ваш проект на одной странице	Стадия	Лист	Листов
Дизайнер	Кырлан А.С.			04.11.26		П	3	127



					Проект: Квартира с кабинетом	
	Лист	№ док.	Подпись	Дата	Визуализация спальни	Стадия / Лист / Листов
Дизайнер	Кырлан А.С.			04.11.26		П / 4 / 127

выпуск 04.11.2026 № 627e1ac6ce · стр. 4 из 127



					Проект: Квартира с кабинетом
	Лист	№ док.	Подпись	Дата	
Дизайнер	Кырлан А.С.			04.11.26	Визуализация спальни

Стадия	Лист	Листов
П	5	127



					Проект: Квартира с кабинетом			
	Лист	№ док.	Подпись	Дата	Визуализация спальни	Стадия	Лист	Листов
Дизайнер	Кырлан А.С.			04.11.26		П	6	127



					Проект: Квартира с кабинетом
	Лист	№ док.	Подпись	Дата	Визуализация: Гардеробная-постирочная
Дизайнер	Кырлан А.С.			04.11.26	

Стадия	Лист	Листов
П	7	127



					Проект: Квартира с кабинетом	
	Лист	№ док.	Подпись	Дата	Визуализация кабинета	Стадия / Лист / Листов
Дизайнер	Кырлан А.С.			04.11.26		П / 8 / 127



					Проект: Квартира с кабинетом
	Лист	№ док.	Подпись	Дата	
Дизайнер	Кырлан А.С.			04.11.26	Визуализация кабинета

Стадия	Лист	Листов
П	9	127



					Проект: Квартира с кабинетом			
	Лист	№ док.	Подпись	Дата	Визуализация кабинета	Стадия	Лист	Листов
Дизайнер	Кырлан А.С.			04.11.26		П	10	127



					Проект: Квартира с кабинетом	
	Лист	№ док.	Подпись	Дата	Визуализация кухни-гостиной	Стадия / Лист / Листов
Дизайнер	Кырлан А.С.			04.11.26		П / 11 / 127



					Проект: Квартира с кабинетом	
	Лист	№ док.	Подпись	Дата	Визуализация кухни-гостиной	Стадия / Лист / Листов
Дизайнер	Кырлан А.С.			04.11.26		П / 12 / 127

выпуск 04.11.2026 № 627e1ac6ce · стр. 12 из 127




					Проект: Квартира с кабинетом	
	Лист	№ док.	Подпись	Дата	Визуализация кухни-гостиной	Стадия / Лист / Листов
Дизайнер	Кырлан А.С.			04.11.26		П / 13 / 127

выпуск 04.11.2026 № 627e1ac6ce · стр. 13 из 127



					Проект: Квартира с кабинетом			
	Лист	№ док.	Подпись	Дата	Визуализация кухни-гостиной	Стадия	Лист	Листов
Дизайнер	Кырлан А.С.			04.11.26		П	14	127

выпуск 04.11.2026 № 627e1ac6ce · стр. 14 из 127

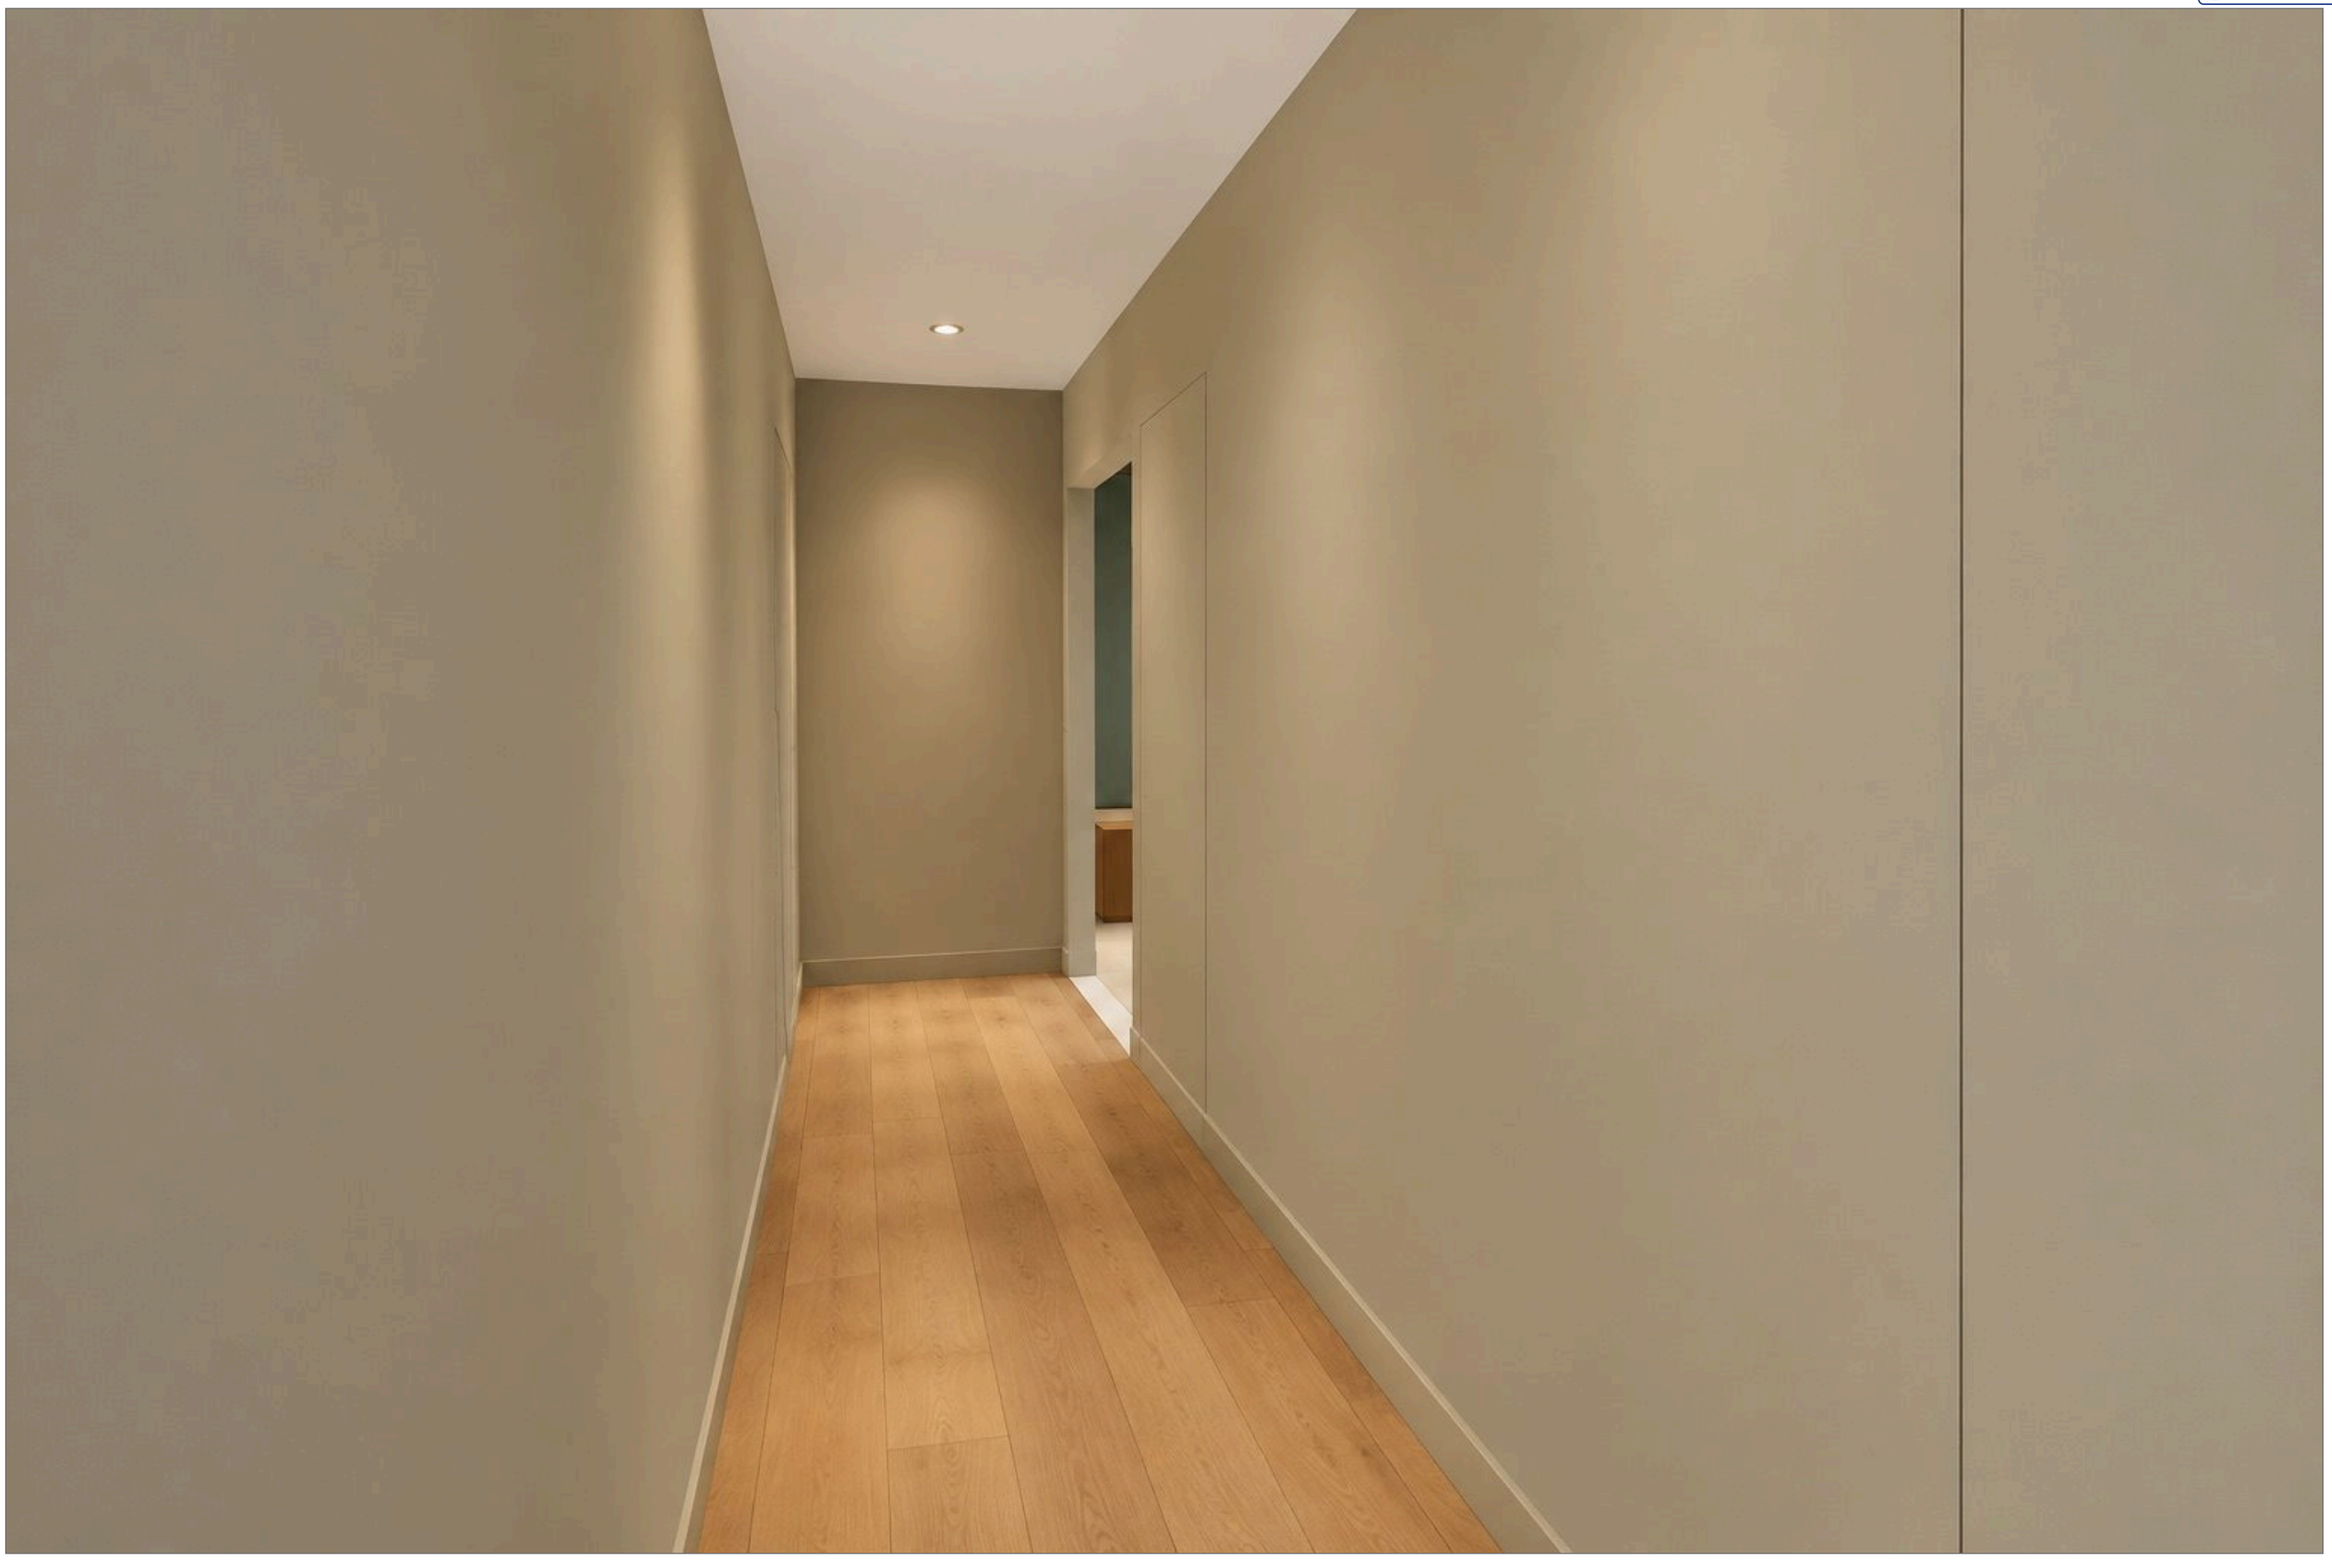

					Проект: Квартира с кабинетом	
	Лист	№ док.	Подпись	Дата		
Дизайнер	Кырлан А.С.			04.11.26	Визуализация коридора	Стадия / Лист / Листов
						П / 15 / 127



					Проект: Квартира с кабинетом	
	Лист	№ док.	Подпись	Дата	Визуализация детской	Стадия / Лист / Листов
Дизайнер	Кырлан А.С.			04.11.26		П / 16 / 127

выпуск 04.11.2026 № 627e1ac6ce · стр. 16 из 127



					Проект: Квартира с кабинетом
	Лист	№ док.	Подпись	Дата	
Дизайнер	Кырлан А.С.			04.11.26	Визуализация детской

Стадия	Лист	Листов
П	17	127



					Проект: Квартира с кабинетом		
	Лист	№ док.	Подпись	Дата	Визуализация детской	Стадия	Лист	Листов
Дизайнер	Кырлан А.С.			04.11.26		П	18	127



					Проект: Квартира с кабинетом	
	Лист	№ док.	Подпись	Дата	Визуализация ванной	Стадия / Лист / Листов
Дизайнер	Кырлан А.С.			04.11.26		П / 19 / 127



					Проект: Квартира с кабинетом			
	Лист	№ док.	Подпись	Дата	Визуализация ванной	Стадия	Лист	Листов
Дизайнер	Кырлан А.С.			04.11.26		П	20	127

выпуск 04.11.2026 № 627e1ac6ce · стр. 20 из 127



					Проект: Квартира с кабинетом	
	Лист	№ док.	Подпись	Дата	Визуализация ванной	Стадия / Лист / Листов
Дизайнер	Кырлан А.С.			04.11.26		П / 21 / 127



					Проект: Квартира с кабинетом	
	Лист	№ док.	Подпись	Дата	Визуализация прихожей	Стадия / Лист / Листов
Дизайнер	Кырлан А.С.			04.11.26		П / 22 / 127



					Проект: Квартира с кабинетом	
	Лист	№ док.	Подпись	Дата	Визуализация прихожей	Стадия / Лист / Листов
Дизайнер	Кырлан А.С.			04.11.26		П / 23 / 127



					Проект: Квартира с кабинетом	
	Лист	№ док.	Подпись	Дата	Визуализация прихожей	Стадия / Лист / Листов
Дизайнер	Кырлан А.С.			04.11.26		П / 24 / 127



					Проект: Квартира с кабинетом
	Лист	№ док.	Подпись	Дата	
Дизайнер	Кырлан А.С.			04.11.26	Визуализация: Санузел гостевой

Стадия	Лист	Листов
П	25	127



					Проект: Квартира с кабинетом			
	Лист	№ док.	Подпись	Дата	Визуализация: Санузел гостевой	Стадия	Лист	Листов
Дизайнер	Кырлан А.С.			04.11.26		П	26	127

Список листов

Лист	Наименование
1	Титульный лист
2	Визуализация. Вид сверху
3	Ваш проект на одной странице
4	Визуализация спальни
5	Визуализация спальни
6	Визуализация спальни
7	Визуализация: Гардеробная-постирочная
8	Визуализация кабинета
9	Визуализация кабинета
10	Визуализация кабинета
11	Визуализация кухни-гостиной
12	Визуализация кухни-гостиной
13	Визуализация кухни-гостиной
14	Визуализация кухни-гостиной
15	Визуализация коридора
16	Визуализация детской
17	Визуализация детской
18	Визуализация детской
19	Визуализация ванной
20	Визуализация ванной
21	Визуализация ванной
22	Визуализация прихожей
23	Визуализация прихожей
24	Визуализация прихожей
25	Визуализация: Санузел гостевой
26	Визуализация: Санузел гостевой
27	Список листов
28	Список листов
29	Как читать альбом
30	План планировки от заказчика
31	План монтажный
32	Кухня (пом. 4). Монтажная схема
33	Шкафы. Монтажная схема. Лист 1 из 2
34	Шкафы. Монтажная схема. Лист 2 из 2
35	Карта покрытий стен
36	Колерная карта
37	План размещения мебели и оборудования
38	Спецификация мебели и оборудования
39	Спецификация мебели и оборудования (продолжение)
40	Спецификация мебели и оборудования (продолжение)
41	Ведомости изделий, техники и фурнитуры
42	План выводов сантехники
43	Схема разводки водопровода и канализации
44	Аксонометрическая схема В1 (холодное водоснабжение)
45	Аксонометрическая схема Т3 (горячее водоснабжение)
46	Аксонометрическая схема К1 (канализация)
47	Развёртки мокрых зон: выводы ВК. Кухня-гостиная
48	Развёртки мокрых зон: выводы ВК. Ванная (лист 1 из 2)
49	Развёртки мокрых зон: выводы ВК. Ванная (лист 2 из 2)
50	Развёртки мокрых зон: выводы ВК. Санузел гостевой (лист 1 из 2)
51	Развёртки мокрых зон: выводы ВК. Санузел гостевой (лист 2 из 2)
52	Спецификация сантехнического оборудования
53	Раскладка плитки. Ванная. Развёртки стен
54	Раскладка плитки. Санузел гостевой. Развёртки стен
55	План размещения дверей
56	Ведомость заполнения проёмов
57	План потолков
58	Разрезы и узлы потолков
59	Разрезы и узлы потолков (продолжение)
60	Разрезы и узлы потолков (продолжение)
61	Сечения потолков М 1:10
62	Сечения потолков М 1:10
63	Однолинейная схема щита
64	Однолинейная схема щита (продолжение)

					Проект: Квартира с кабинетом
	Лист	№ док.	Подпись	Дата	Список листов
Дизайнер	Кырлан А.С.			04.11.26	Стадия: П; Лист: 27; Листов: 127

Список листов (продолжение)

Лист	Наименование
65	План розеток и электровыводов
66	План слаботочных сетей
67	План освещения
68	Техническое задание на подбор светильников
69	Управление светильниками
70	План вентиляции
71	План отопления
72	План покрытий пола
73	Раскладка плитки. Планы полов
74	Раскладка плитки. Прихожая. Фартук кухни
75	Развёртка стены А. Спальня (пом. 1)
76	Развёртка стены Б. Спальня (пом. 1)
77	Привязки электроточек, стена Б. Спальня (пом. 1)
78	Развёртка стены В. Спальня (пом. 1)
79	Развёртка стены Г. Спальня (пом. 1)
80	Развёртки стен А, Б. Гардеробная-постирочная (пом. 2)
81	Развёртки стен В, Г. Гардеробная-постирочная (пом. 2)
82	Развёртка стены А. Кабинет (пом. 3)
83	Развёртка стены Б. Кабинет (пом. 3)
84	Развёртка стены В. Кабинет (пом. 3)
85	Развёртка стены Г. Кабинет (пом. 3)
86	Развёртка стены Г. Кухня-гостиная (пом. 4), кухонный фронт
87	Привязки электроточек, стена Г. Кухня-гостиная (пом. 4)
88	Развёртка стены А. Кухня-гостиная (пом. 4), кухонный фронт
89	Привязки электроточек и выводов ВК, стена А. Кухня-гостиная (пом. 4)
90	Развёртка стены Б. Кухня-гостиная (пом. 4)
91	Привязки электроточек, стена Б. Кухня-гостиная (пом. 4)
92	Развёртка стены В. Кухня-гостиная (пом. 4)
93	Развёртки стен А1, Г. Коридор (пом. 5)
94	Развёртка стены А2. Коридор (пом. 5)
95	Развёртка стены В. Коридор (пом. 5)
96	Развёртка стены А. Детская (пом. 6)
97	Развёртка стены Б. Детская (пом. 6)
98	Привязки электроточек, стена Б. Детская (пом. 6)
99	Развёртка стены В. Детская (пом. 6)
100	Развёртка стены Г. Детская (пом. 6)
101	Развёртки стен А, Б. Ванная (пом. 7)
102	Развёртки стен В, Г. Ванная (пом. 7)
103	Привязки электроточек и выводов ВК, стены Б, Г. Ванная (пом. 7)
104	Развёртки стен Б, В. Прихожая (пом. 8)
105	Развёртка стены Г. Прихожая (пом. 8)
106	Развёртки стен А, Б. Санузел гостевой (пом. 9)
107	Привязки электроточек и выводов ВК, стена А. Санузел гостевой (пом. 9)
108	Развёртки стен В, Г. Санузел гостевой (пом. 9)
109	Открытые вопросы, принятые допущения и конфликты. Лист 1 из 3
110	Открытые вопросы, принятые допущения и конфликты. Лист 2 из 3
111	Открытые вопросы, принятые допущения и конфликты. Лист 3 из 3
Д_1	Система хранения M_06
Д_2	Система хранения M_07
Д_3	Шкаф распашной M_08
Д_4	ТВ-стена M_24
Д_5	Шкаф распашной M_25
Д_6	Шкаф распашной M_26
Д_7	Тумба под раковину M_29
Д_8	Шкаф-купе M_30
Д_9	Кухня (пом. 4). Развёртка гарнитура
Д_10	Остров M_19 (пом. 4). Чертёж изделия
С1	Ведомость отделки помещений. Лист 1 из 2
С2	Ведомость отделки помещений. Лист 2 из 2
С3	Спецификация отделочных материалов
С4	Список покупок
С5	Список покупок (окончание)
С6	Узлы

Общие указания

1. Размеры даны в мм от чистовых поверхностей стен: слой штукатурки 20 мм по блоку и 5 мм шпаклёвки по ГКЛ учтён. Перед заказом встроенной мебели — контрольный обмер после штукатурки.
2. Привязки мебели — от стен и углов помещения, а не от другой мебели.
3. Розетки, выводы и выключатели под мебель — см. лист 65 «План розеток и электровыводов»; сантехприборы и выводы воды — лист 42.
4. План расстановки не является документацией для изготовления мебели: изделия — по чертежам мебельщика; покупную мебель заменять только на изделия не больше габарита из спецификации (лист 38).
5. Встроенная мебель «стена в стену» — с зазором 10 мм с каждой стороны или с компенсаторами.
6. Развёртки — вид на стену изнутри помещения, по часовой стрелке; расположение стен на схеме листа развёртки; размеры — в мм по чистовым поверхностям; отметки — в м от ±0,000; высоты H — от чистого пола помещения до оси изделия, у декора — до центра.
7. Красная цепочка — привязки электроточек и выводов по осям от угла чистовых стен; высота H — у знака, от чистого пола до оси; высоты мебели, проёмов и границ отделки колонкой отметок слева. Стена с 5 и более точками или с мелкими звеньями привязок показана двумя видами: архитектурная развёртка (мебель, отделка, проёмы, высоты) и вид «Привязки» на отдельном листе — точки и выводы с марками, одна цепочка по осям и таблица привязок (каждая точка — строка).
8. У знака электроточки: марка (Р — розетка, S — выключатель, Св — светильник, ЭВ вывод кабеля), ×N — число постов в рамке, гр. — группа щита, H — высота оси от чистого пола, мм; группы по клавишам выключателя — на листе выключателей.
9. Схема мебели, приборов и декора не является технической документацией для производства мебели; габариты — по паспортам изделий.
10. Марки позиций: M_NN — мебель, ОБ_NN — оборудование, С_NN — сантехника; О-N отделка (ведомость отделочных материалов, серия С).
11. Размеры мебели и изделий на заказ уточнить по месту после отделочных работ.

					Проект: Квартира с кабинетом
	Лист	№ док.	Подпись	Дата	Список листов
Дизайнер	Кырлан А.С.			04.11.26	

Стадия	Лист	Листов
П	28	127

Что в альбоме

Альбом — дизайн-проект с рабочими чертежами для ремонта. Листы идут в порядке работ: титул и вводные, реестр открытых вопросов и решений, планы (обмер, монтаж стен, мебель, двери, потолки, полы), инженерия (сантехника, электрика, вентиляция и отопление), развёртки стен с визуализациями помещений, чертежи мебели, ведомости материалов и узлы.

Вам как заказчику — титул, эта вводная, «Ваш проект на одной странице», реестр вопросов, план мебели, визуализации и развёртки, ведомости мебели и материалов. Подрядчику — всё остальное: монтажные планы, привязки выводов и розеток, узлы, ведомости объёмов.

Знаки на листах

Без знака — решение утверждено или подтверждено обмером.

Что проверить до ремонта

1. Розетки у кровати и рабочего места: хватает ли их с каждой стороны кровати и над столом (план розеток — лист 65).

2. Выводы под технику — варочная панель, духовка, посудомойка, стиральная машина, бойлер: совпадают ли с выбранными моделями (листы 38, 39, 40, 65).

3. Высоты розеток, выключателей и выводов даны от чистого пола: если мебель или техника будут другими — скажите до штробления стен.

Номера записей

К-N — открытый вопрос: чего не хватает или что выбрать (варианты и рекомендация — в тексте). Пока ответа нет, действует строка «если решения нет».

Кф-N — конфликт между разделами (например, мебель и радиатор в одном месте); закрывается решением, которое записывается как ИЗ-N.

ИЗ-N — изменение проекта: что было, что стало и кто утвердил. Изменение без подписи предложение.

Все записи — на листе реестра сразу после вводных; на других листах на них стоят ссылки.

Почему альбом предварительный

Обмера на объекте не было: размеры взяты с плана заказчика. Технические условия (мощность, вода, вентиляция дома) не получены, часть решений ждёт вашего ответа. Пока в реестре есть открытые вопросы, альбом предварительный — пометка в штампе снимается закрытием вопросов, а не стиранием.

Правку к любому листу можно оставить по кнопке «Правка к листу» или на сайте студии: дизайн-студия-квартир.рф — укажите номер листа и что изменить.

3 круга правок входят в цену; условия — в договоре и на странице вашего заказа на сайте студии.


Шифр проекта ГД-2026-008-АИ

					Проект: Квартира с кабинетом
	Лист	№ док.	Подпись	Дата	
Дизайнер	Кырлан А.С.			04.11.26	Как читать альбом
					Стадия: П; Лист: 29; Листов: 127

выпуск 04.11.2026 № 627e1ac6ce · стр. 29 из 127

Отметки по высоте

±0,000 чистый пол пом. 1–6, 8; отсчёт высот
−0,015 чистый пол пом. 7, 9, ниже на 15 мм
−0,064 верх плиты — расчёт, не замер (задание на обмер)
сущ. пол снимается до плиты; не замерен (задание на обмер)

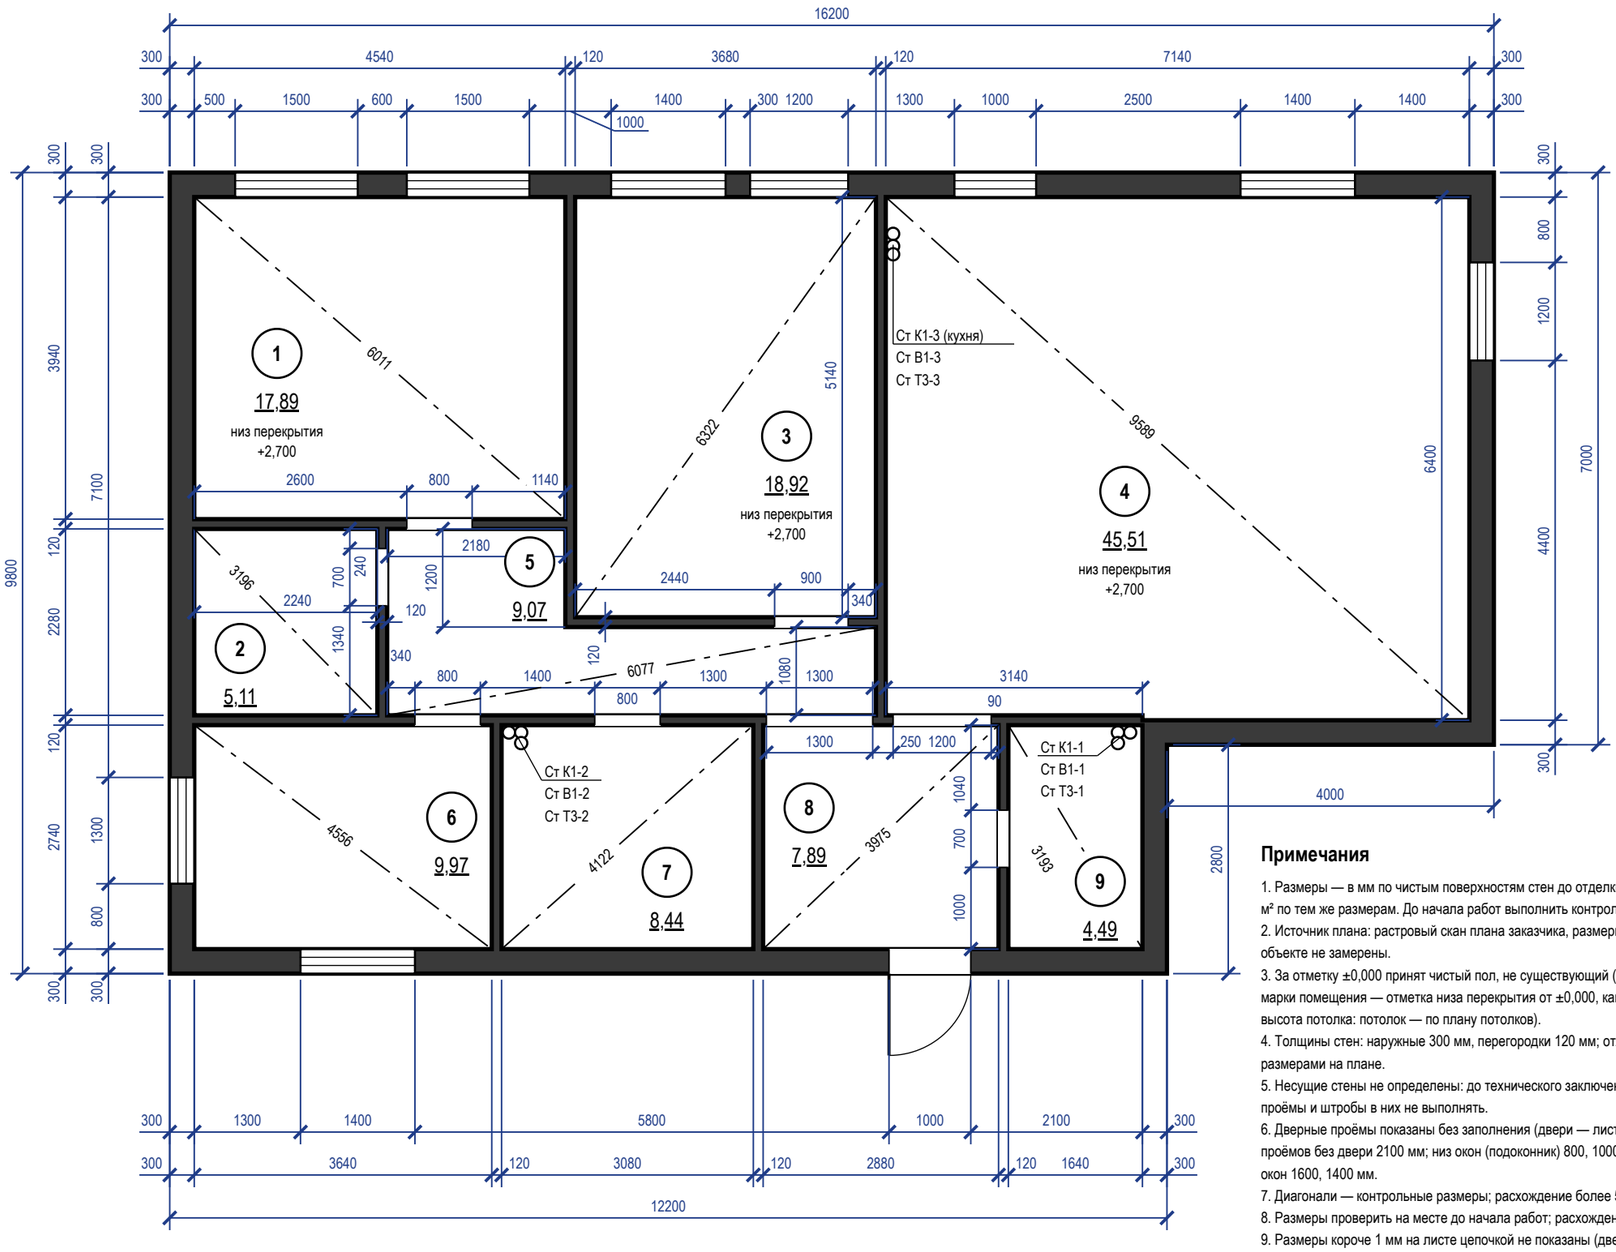

Экспликация помещений

№	Наименование	Площадь, м²
1	Спальня	17,89
2	Гардеробная-постирочная	5,11
3	Кабинет	18,92
4	Кухня-гостиная	45,51
5	Коридор	9,07
6	Детская	9,97
7	Ванная	8,44
8	Прихожая	7,89
9	Санузел гостевой	4,49
	Итого (общая площадь)	**127,29**

Условные обозначения


- существующие стены (сечение)
- окно (рама, остекление)
- проём существующий, без заполнения (откосы)
- стояк: К1 — канализация, В1 — ХВС, Т3 — ГВС
- диагональ помещения — контроль прямоугольности
- (1) номер помещения, площадь м²

Примечания

1. Размеры — в мм по чистым поверхностям стен до отделки (по плану заказчика); площади — в м² по тем же размерам. До начала работ выполнить контрольный обмер.
2. Источник плана: растровый скан плана заказчика, размеры сняты с размерных цепочек, на объекте не замерены.
3. За отметку ±0,000 принят чистый пол, не существующий (блок отметок). «Низ перекрытия» у марки помещения — отметка низа перекрытия от ±0,000, как на развёртках и плане потолков (не высота потолка: потолок — по плану потолков).
4. Толщины стен: наружные 300 мм, перегородки 120 мм; отличающиеся толщины и уступы размерами на плане.
5. Несущие стены не определены: до технического заключения все стены считать несущими; проёмы и штробы в них не выполнять.
6. Дверные проёмы показаны без заполнения (двери — лист 56); высота дверных проёмов 2100 мм, проёмов без двери 2100 мм; низ окон (подоконник) 800, 1000, 900 мм от чистого пола, высота окон 1600, 1400 мм.
7. Диагонали — контрольные размеры; расхождение более 5 мм подписать на плане как перекос.
8. Размеры проверить на месте до начала работ; расхождение контрольных промеров ≤ 2 %.
9. Размеры короче 1 мм на листе цепочкой не показаны (две выносные линии на таком расстоянии сливаются): пом. 5, стена В — 40 мм от проёма до угла; пом. 8, стена А — 40 мм от угла до проёма.

					Проект: Квартира с кабинетом	**М 1:75**
	Лист	№ док.	Подпись	Дата	План планировки от заказчика	Стадия / Лист / Листов
Дизайнер	Кырлан А.С.			04.11.26		П / 30 / 127

выпуск 04.11.2026 № 627e1ac6ce · стр. 30 из 127

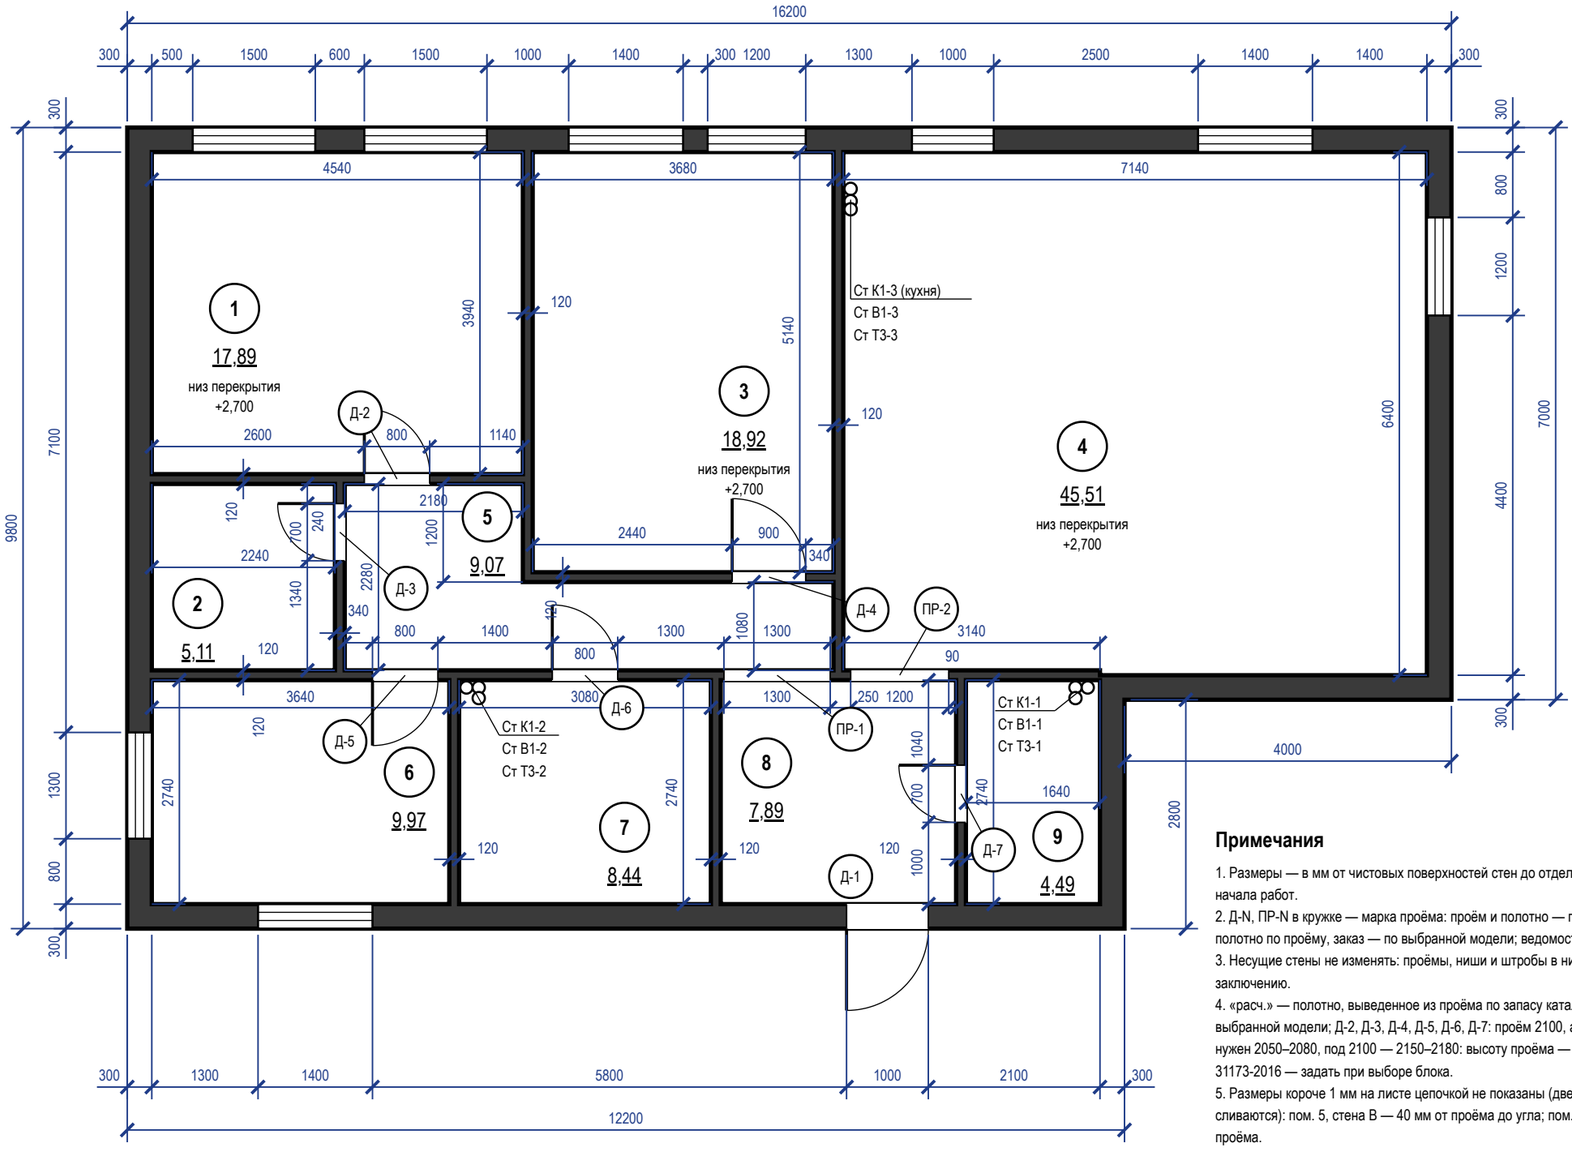

Экспликация помещений

№	Наименование	Площадь, м²
1	Спальня	17,89
2	Гардеробная-постирочная	5,11
3	Кабинет	18,92
4	Кухня-гостиная	45,51
5	Коридор	9,07
6	Детская	9,97
7	Ванная	8,44
8	Прихожая	7,89
9	Санузел гостевой	4,49
	Итого (общая площадь)	**127,29**

Таблица проёмов


Марка	Наименование	Проём ш×в, мм	Полотно (расч.)
Д-1	Дверь входная	1000×2100	блок — задать
Д-2	Дверь скрытого монтажа	800×2100	700×2000
Д-3	Дверь скрытого монтажа	700×2100	600×2000
Д-4	Дверь скрытого монтажа	900×2100	800×2000
Д-5	Дверь скрытого монтажа	800×2100	700×2000
Д-6	Дверь скрытого монтажа	800×2100	700×2000
Д-7	Дверь скрытого монтажа	700×2100	600×2000
ПР-1	Проём без заполнения	1300×2100	
ПР-2	Проём без заполнения	1200×2100	

Примечания


1. Размеры — в мм от чистовых поверхностей стен до отделки; размеры уточнить по месту до начала работ.
2. Д-N, ПР-N в кружке — марка проёма: проём и полотно — по таблице проёмов, «расч.» полотно по проёму, заказ — по выбранной модели; ведомость, отделка и фурнитура — лист 56.
3. Несущие стены не изменять: проёмы, ниши и штробы в них — только по техническому заключению.
4. «расч.» — полотно, выведенное из проёма по запасу каталогов; заказ — по таблице проёмов выбранной модели; Д-2, Д-3, Д-4, Д-5, Д-6, Д-7: проём 2100, а под полотно 2000 по каталогам нужен 2050–2080, под 2100 — 2150–2180: высоту проёма — по модели; Д-1: входной блок по ГОСТ 31173-2016 — задать при выборе блока.
5. Размеры короче 1 мм на листе цепочкой не показаны (две выносные линии на таком расстоянии сливаются): пом. 5, стена В — 40 мм от проёма до угла; пом. 8, стена А — 40 мм от угла до проёма.

					Проект: Квартира с кабинетом	М 1:75
	Лист	№ док.	Подпись	Дата	План монтажный	Стадия / Лист / Листов
Дизайнер	Кырлан А.С.			04.11.26		П / 31 / 127

Привязка выводов и крепление модулей

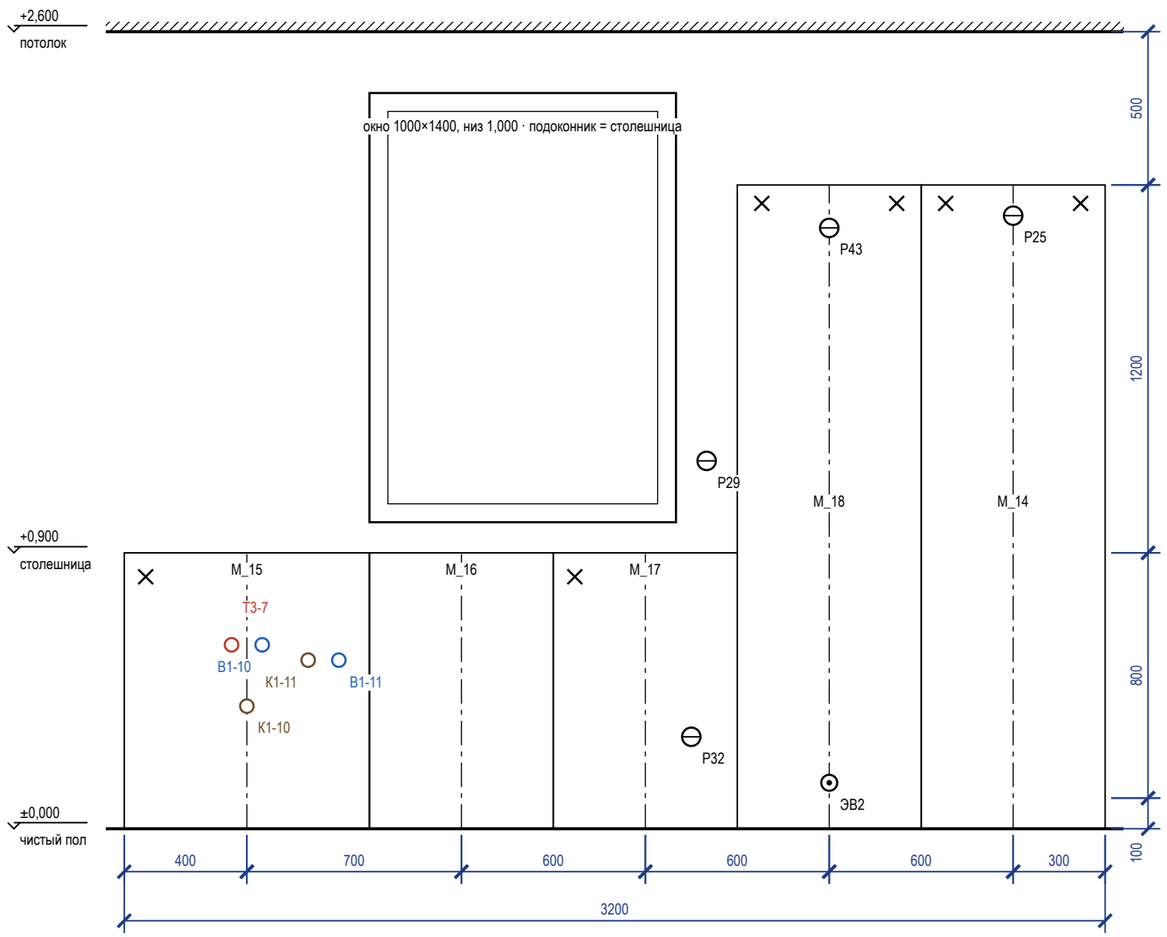

План столешницы

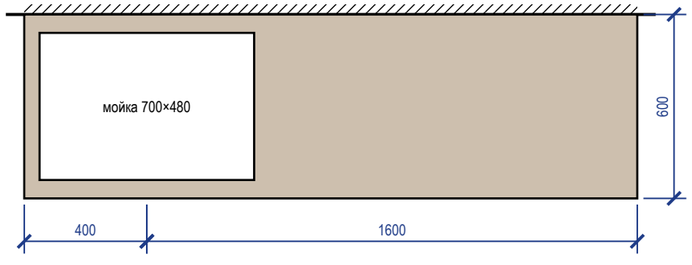

Привязка выводов к осям модулей

Код	Назначение	Модуль	От оси, мм	H, мм	Размещение
T3-7	T3 — межос. 100	M_15	−50	600	в модуле мойки
K1-10	K1 Ø50 — мойка	M_15	0	400	в модуле мойки
B1-10	B1 — межос. 100	M_15	+50	600	в модуле мойки
K1-11	K1 Ø40 — слив ПММ в шкафу мойки	M_15	+200	550	в модуле мойки
B1-11	B1 — кран ПММ в шкафу мойки	M_15	+300	550	в модуле мойки
P32	розетка — посудомоечная машина — в соседнем модуле, за ящиком	M_17	+150	300	в соседнем модуле, за ящиком
P29	розетка — фартук	M_17	+200	1200	над столешницей (фартук)
ЭВ2	вывод кабеля — духовой шкаф — в цоколе	M_18	0	150	за ящиком под нишей, доступ через ящик
P43	розетка — СВЧ — над нишей, съёмная панель	M_18	0	1960	над нишами техники, за съёмной панелью антресоли
P25	розетка — холодильник — над нишей, съёмная панель	M_14	0	2000	над нишей холодильника, съёмная панель

Зазоры под отделку

Поверхность	Отделка	Зазор, мм	Учесть
фартук	керамогранит	10	от чернового основания до корпуса навесных и столешницы
стены	окраска	5	под штукатурку и шпаклёвку за пеналом
пол	инженерная доска		цоколь — после укладки пола, опоры ±20 мм

Условные обозначения


- нижний модуль, пенал (контур)
- ось модуля (от неё — привязка вывода)
- анкер / уголок крепления к стене
- розетка на стене
- вывод кабеля к технике
- B1 — вывод воды B1 / T3, канализации K1

Примечания


1. Окно над M_16, M_17: низ проёма на 1000 мм от пола, столешница на 900 мм; примыкание столешницы к откосу и подоконнику — до решения: нужно решение заказчика (створка глухая или поворотно-откидная, поднять подоконник); столешницу у окна не раскраивать до решения.
2. Выводы — по проекту электрики и ВК; привязка по горизонтали — от оси модуля (плюс — вправо по виду), по высоте — от чистого пола до оси вывода.
3. Пенал — уголки к стене 2 шт. сверху; нижние модули — стяжками между собой и уголком к стене; ряд выставить по уровню опорами цоколя.
4. Розетки над столешницей — не ниже 150 мм над ней и не за корпусом техники; розетка за ПММ, духовым шкафом и холодильником — только в соседнем модуле или в зоне цоколя с доступом.
5. Столешница — вырезы по шаблонам выбранных моделей мойки и варочной панели; торцы у стены — герметик, пристеночный плинтус.

					Проект: Квартира с кабинетом — **M 1:20**
	Лист	№ док.	Подпись	Дата	Кухня (пом. 4). Монтажная схема
Дизайнер	Кырлан А.С.			04.11.26	Стадия: П · Лист: 32 · Листов: 127


Система хранения M_06 (пом. 2)

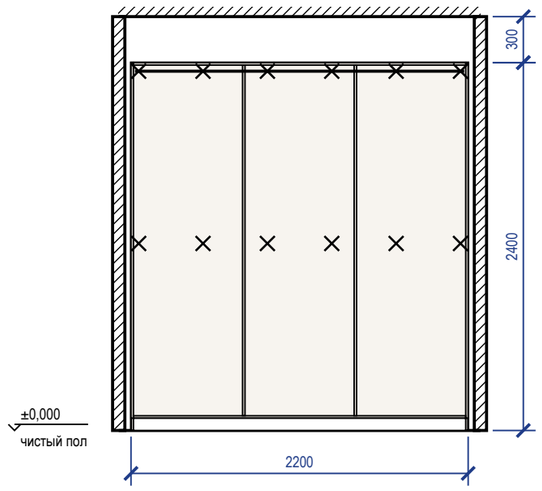


Система хранения M_07 (пом. 2)

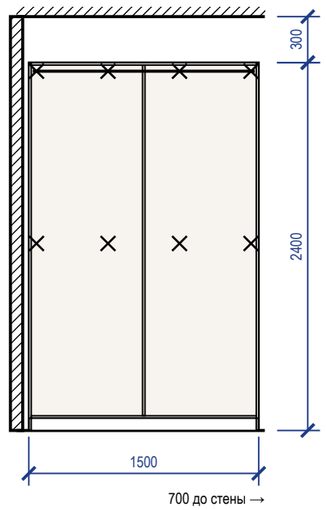

Шкаф распашной M_08 (пом. 3)

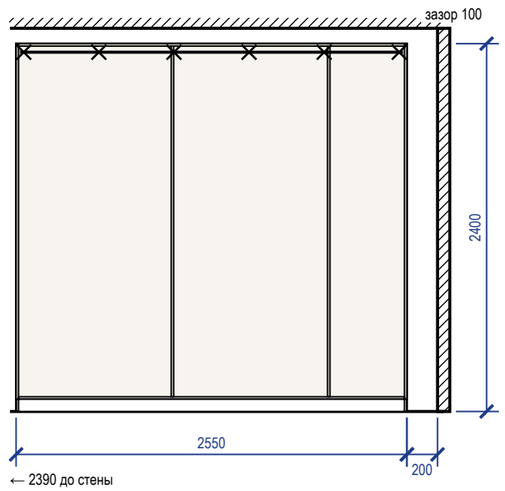

ТВ-стена M_24 (пом. 4)

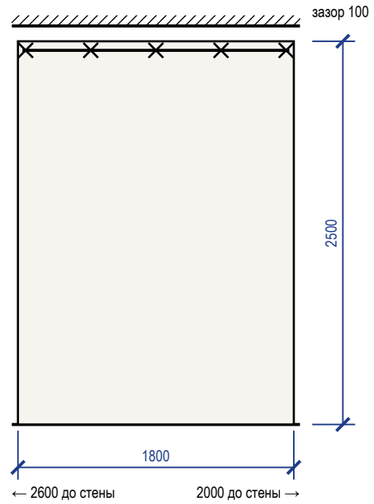

Крепление и зазоры под отделку (изделия листа 1)

Марка	Помещение, стена	Основание	Отделка стены	Зазор, мм	Крепёж по планке	От опрокидывания
M_06	Гардеробная-постирочная (2), стена Г	по основанию — см. таблицу крепежа	окраска	5	анкер 12 шт. (2 ряда)	крепление к стене, 3 точки
M_07	Гардеробная-постирочная (2), стена В	по основанию — см. таблицу крепежа	окраска	5	анкер 8 шт. (2 ряда)	крепление к стене, 3 точки
M_08	Кабинет (3), стена Г	по основанию — см. таблицу крепежа	окраска	5	анкер 6 шт., шаг 490	уголки 2 шт.
M_24	Кухня-гостиная (4), стена Б	по основанию — см. таблицу крепежа	окраска	5	анкер 5 шт., шаг 425	уголки 2 шт.

Крепёж по основанию стены

Основание стены	Крепёж
бетон, ж/б	анкер-шуруп 7,5×72 или дюбель 8×60 с шурупом 5×70
кирпич полнотелый	дюбель 8×80 с шурупом 5×90
газобетон, пазогребень	дюбель для газобетона 10×100 или химический анкер
гипсокартон	закладная до обшивки (брус 40×80 или фанера 18 мм), саморез в закладную

Условные обозначения


- × — анкер / уголок крепления к стене
- прямоугольник — корпус и полки ЛДСП (вид на стену)
- штриховка — компенсатор — короб до потолка

Примечания


1. Установочные размеры — от чистого пола и чистых стен; перед установкой контрольный замер после отделки.
2. Порядок: корпус выставить по уровню опорами цоколя → закрепить к стене по задней планке → навесить двери и фасады, отрегулировать зазоры → подогнать и закрепить компенсатор.
3. Анкеры — с шагом не более 500 мм, не ближе 50 мм от края планки; на ГКЛ только в закладную, установленную до обшивки.
4. Скрытые коммуникации под анкеры проверить детектором; трассы электрики по плану розеток.
5. Сборка стоя на месте: M_24 — корпус не собирается лёжа и не поднимается собранным, а собирается в проектном положении у стены; выставление по уровню и крепление к стене выполняются по корпусу, собранному на месте.
6. Монтажная схема на 2 листах, лист 1 из 2; продолжение — на следующем листе схемы. Условные обозначения, таблица крепежа по основанию и примечания повторены на каждом листе.

					Проект: Квартира с кабинетом	**M 1:40**
	Лист	№ док.	Подпись	Дата		
Дизайнер	Кырлан А.С.			04.11.26	Шкафы. Монтажная схема. Лист 1 из 2	Стадия: П; Лист: 33; Листов: 127


Шкаф распашной М_25 (пом. 4)

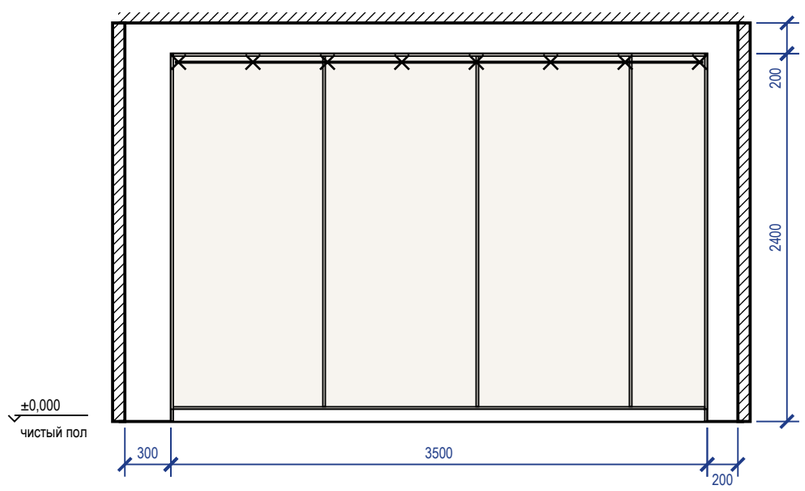


Шкаф распашной М_26 (пом. 6)

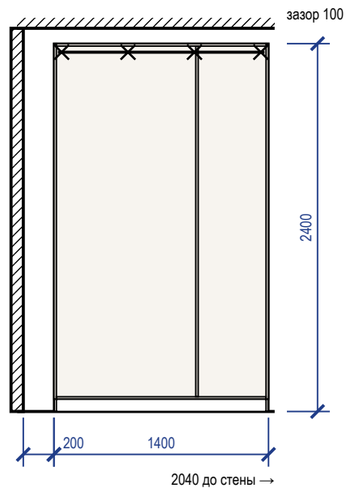

Тумба под раковину М_29 (пом. 7)

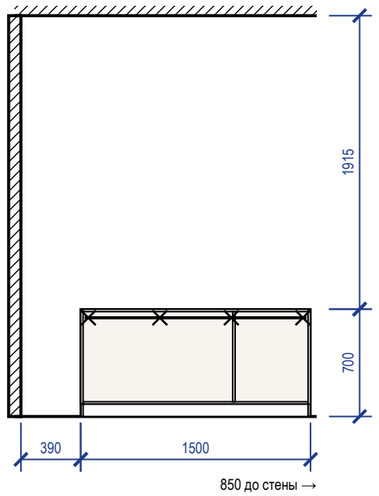

Шкаф-купе М_30 (пом. 8)

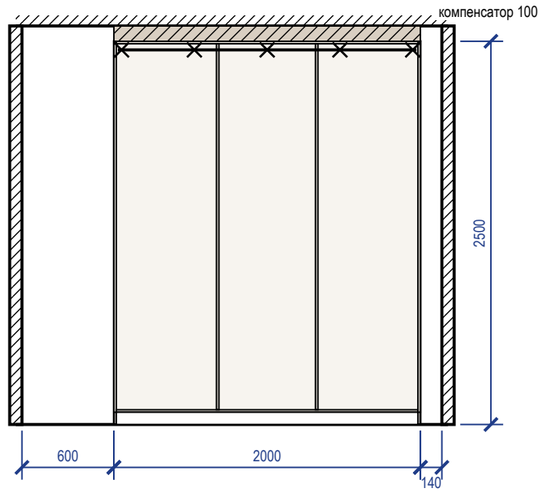

Крепление и зазоры под отделку (изделия листа 2)

Марка	Помещение, стена	Основание	Отделка стены	Зазор, мм	Крепёж по планке	От опрокидывания
М_25	Кухня-гостиная (4), стена В	по основанию — см. таблицу крепежа	окраска	5	анкер 8 шт., шаг 486	уголки 2 шт.
М_26	Детская (6), стена А	по основанию — см. таблицу крепежа	окраска	5	анкер 4 шт., шаг 433	крепление к стене, 2 точки
М_29	Ванная (7), стена Б	по основанию — см. таблицу крепежа	плитка	10	анкер 4 шт., шаг 467	крепление к стене, 2 точки
М_30	Прихожая (8), стена Г	по основанию — см. таблицу крепежа	окраска	5	анкер 5 шт., шаг 475	уголки 2 шт.

Крепёж по основанию стены

Основание стены	Крепёж
бетон, ж/б	анкер-шуруп 7,5×72 или дюбель 8×60 с шурупом 5×70
кирпич полнотелый	дюбель 8×80 с шурупом 5×90
газобетон, пазогребень	дюбель для газобетона 10×100 или химический анкер
гипсокартон	закладная до обшивки (брус 40×80 или фанера 18 мм), саморез в закладную


Условные обозначения

- × — анкер / уголок крепления к стене
- прямоугольник — корпус и полки ЛДСП (вид на стену)
- штриховка — компенсатор — короб до потолка

Примечания

1. Установочные размеры — от чистого пола и чистых стен; перед установкой контрольный замер после отделки.
2. Порядок: корпус выставить по уровню опорами цоколя → закрепить к стене по задней планке → навесить двери и фасады, отрегулировать зазоры → подогнать и закрепить компенсатор.
3. Анкеры — с шагом не более 500 мм, не ближе 50 мм от края планки; на ГКЛ только в закладную, установленную до обшивки.
4. Скрытые коммуникации под анкеры проверить детектором; трассы электрики по плану розеток.
5. Монтажная схема на 2 листах, лист 2 из 2. Условные обозначения, таблица крепежа по основанию и примечания повторены на каждом листе.

					Проект: Квартира с кабинетом	М 1:40
	Лист	№ док.	Подпись	Дата		
Дизайнер	Кырлан А.С.			04.11.26	Шкафы. Монтажная схема. Лист 2 из 2	Стадия: П; Лист: 34; Листов: 127

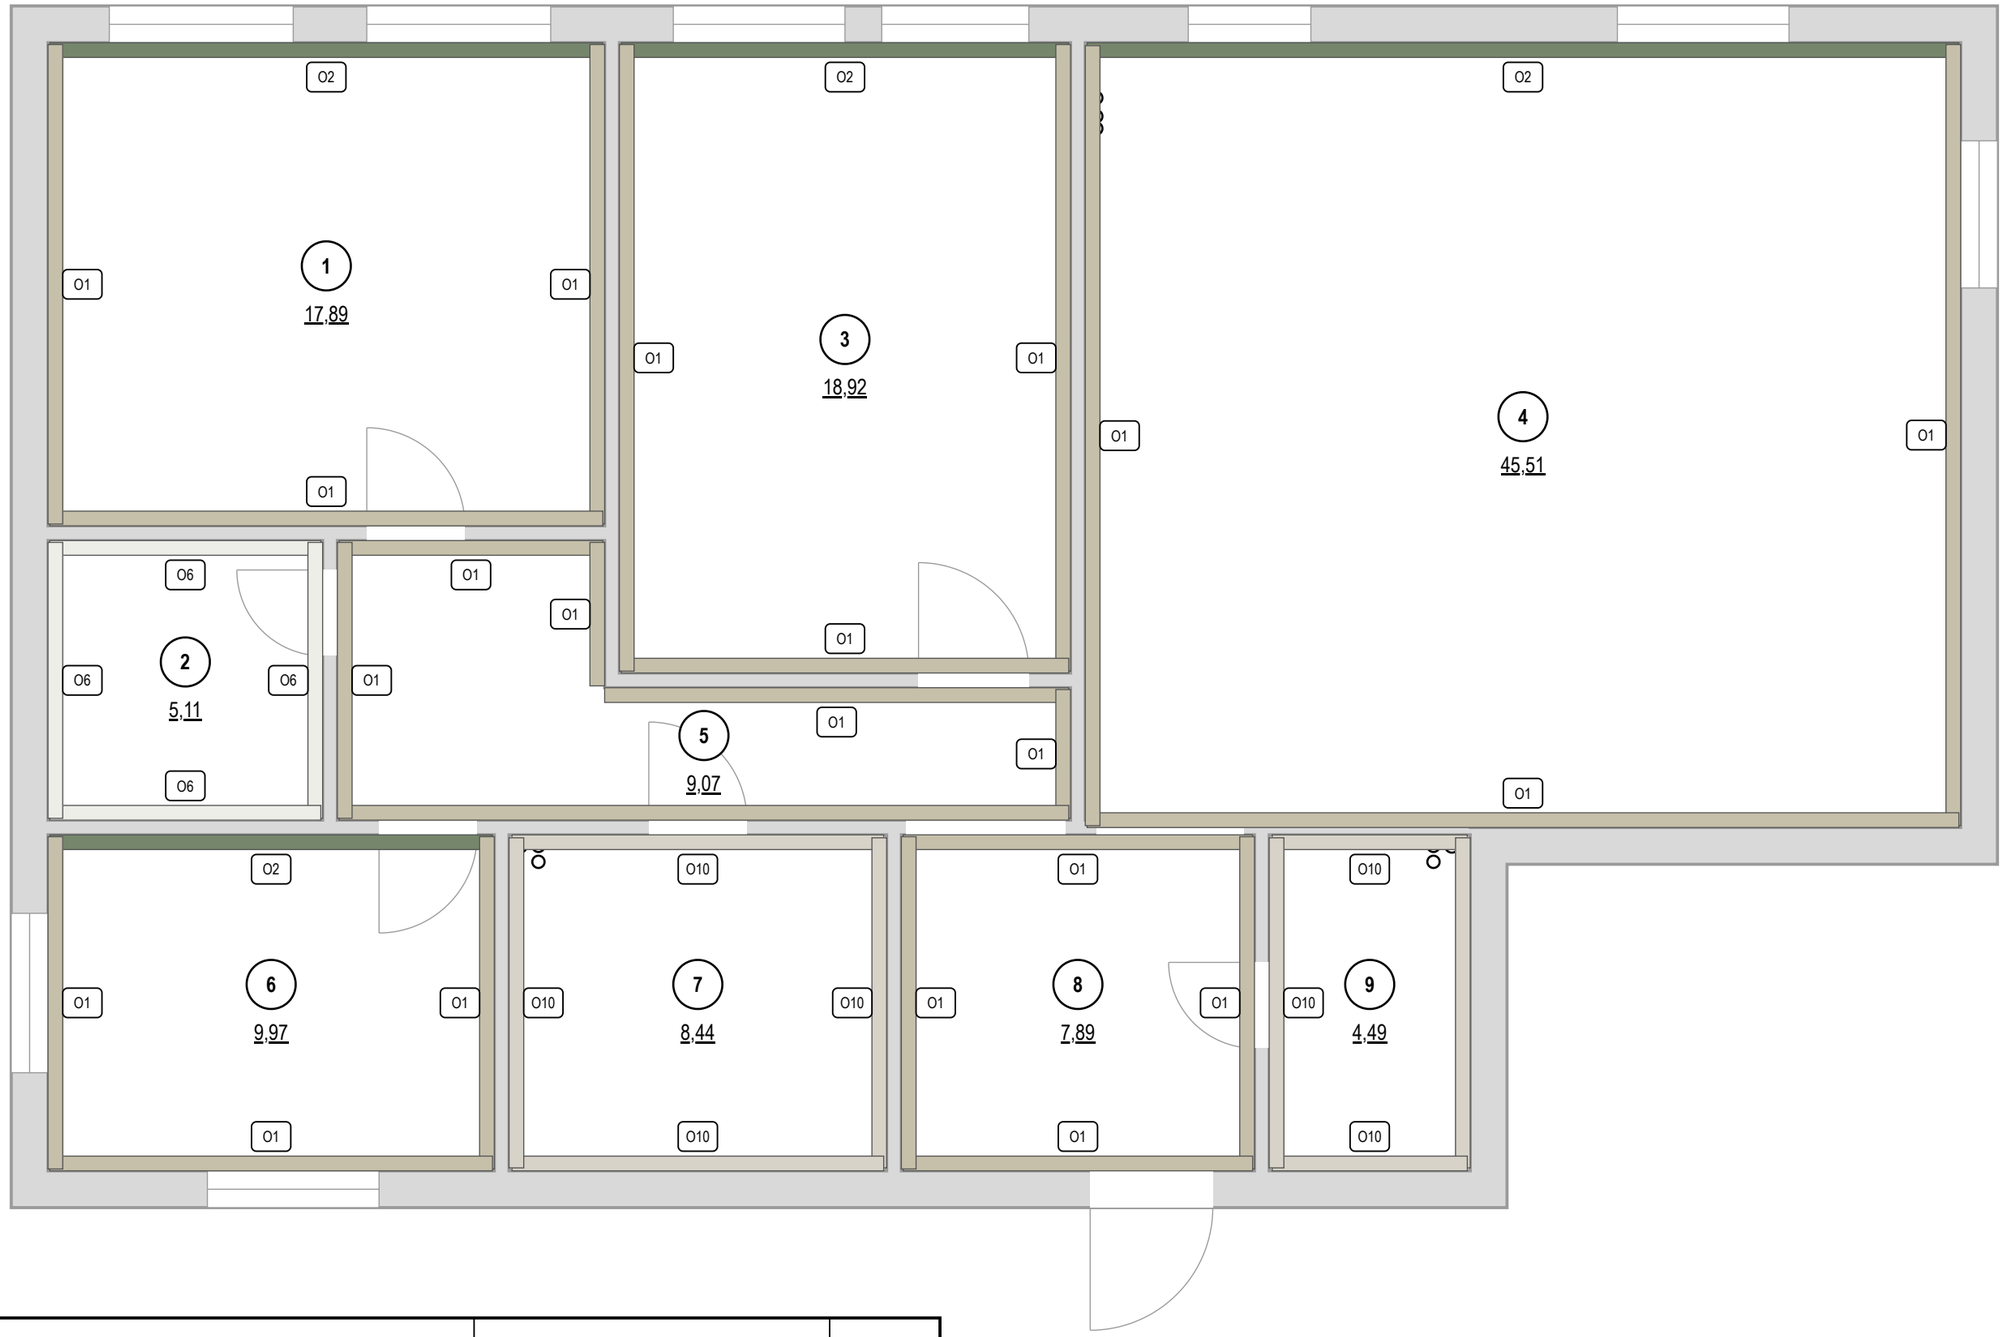

Покрытия стен

Марка	Покрытие	Помещение: S, м²	Итого, м²
O1	окраска Farrow & Ball · No. 15 «Bone — мягкий каменно-серый с зеленцой»	1: 29,1; 3: 32,8; 4: 47,8; 5: 31,4; 6: 18,9; 8: 20,1	180,1
O2	окраска Farrow & Ball · No. 34 «Calke Green — традиционный шалфей»	1: 6,9; 3: 5,3; 4: 14,4; 6: 7,3	34,0
O6	окраска Tikkurila · V503 «Winter»	2: 22,6	22,6
O10	облицовка плиткой Atlas Concorde · A8UZ «Marvel Travertine» 600×1200 мм	7: 28,3; 9: 20,9	49,2

Площади — нетто, по развёрткам (за вычетом проёмов и фартука); высоты помещений — от чистого пола.

					Проект: Квартира с кабинетом — **М 1:50**
	Лист	№ док.	Подпись	Дата	Карта покрытий стен — Стадия: П; Лист: 35; Листов: 127
Дизайнер	Кырлан А.С.			04.11.26	

Колерная карта по помещениям

Помещение	Поверхность	Образец	Поз.	Система и код цвета	Производитель, линейка / материал, артикул	Блеск	Класс истирания	LRV	Площадь
1. Спальня 17,89 м²	стены		**K1**	Farrow & Ball No. 15	Farrow & Ball · Modern Emulsion	матовая	1	53	29,4 м²
	акцент А		**K2**	Farrow & Ball No. 34	Farrow & Ball · Modern Emulsion	матовая	1	22	6,5 м²
	потолок		**K3**	Tikkurila V503	Tikkurila · Anti-Reflex 2	глубокомат.	2	86	17,9 м²
	пол		**KM1**	по образцу	Coswick · Вековые традиции · арт. 1167-4250				17,9 м²
	плинтус		**K4**	Farrow & Ball No. 15	МДФ · в цвет Farrow & Ball			53	16,2 м
2. Гардеробная-постирочная 5,11 м²	стены		**K5**	Tikkurila V503	Tikkurila · Harmony	матовая	1	86	22,9 м²
	потолок		**K3**	Tikkurila V503	Tikkurila · Anti-Reflex 2	глубокомат.	2	86	5,1 м²
	пол		**KM1**	по образцу	Coswick · Вековые традиции · арт. 1167-4250				5,1 м²
	плинтус		**K6**	Tikkurila V503	МДФ · в цвет Tikkurila			86	8,3 м
3. Кабинет 18,92 м²	стены		**K1**	Farrow & Ball No. 15	Farrow & Ball · Modern Emulsion	матовая	1	53	33,0 м²
	акцент А		**K2**	Farrow & Ball No. 34	Farrow & Ball · Modern Emulsion	матовая	1	22	5,0 м²
	потолок		**K3**	Tikkurila V503	Tikkurila · Anti-Reflex 2	глубокомат.	2	86	18,9 м²
	пол		**KM1**	по образцу	Coswick · Вековые традиции · арт. 1167-4250				18,9 м²
	плинтус		**K4**	Farrow & Ball No. 15	МДФ · в цвет Farrow & Ball			53	16,7 м
4. Кухня-гостиная 45,51 м²	стены		**K1**	Farrow & Ball No. 15	Farrow & Ball · Modern Emulsion	матовая	1	53	46,7 м²
	акцент А		**K2**	Farrow & Ball No. 34	Farrow & Ball · Modern Emulsion	матовая	1	22	14,9 м²
	потолок		**K3**	Tikkurila V503	Tikkurila · Anti-Reflex 2	глубокомат.	2	86	45,5 м²
	пол		**KM1**	по образцу	Coswick · Вековые традиции · арт. 1167-4250				45,5 м²
	плинтус		**K4**	Farrow & Ball No. 15	МДФ · в цвет Farrow & Ball			53	25,9 м
	фартук		**KM2**	по образцу	керамогранит · аналог по хар.				0,7 м²
5. Коридор 9,07 м²	стены		**K1**	Farrow & Ball No. 15	Farrow & Ball · Modern Emulsion	матовая	1	53	31,8 м²
	потолок		**K3**	Tikkurila V503	Tikkurila · Anti-Reflex 2	глубокомат.	2	86	9,1 м²
	пол		**KM1**	по образцу	Coswick · Вековые традиции · арт. 1167-4250				9,1 м²
	плинтус		**K4**	Farrow & Ball No. 15	МДФ · в цвет Farrow & Ball			53	11,2 м
6. Детская 9,97 м²	стены		**K1**	Farrow & Ball No. 15	Farrow & Ball · Modern Emulsion	матовая	1	53	18,5 м²
	акцент А		**K2**	Farrow & Ball No. 34	Farrow & Ball · Modern Emulsion	матовая	1	22	7,4 м²
	потолок		**K3**	Tikkurila V503	Tikkurila · Anti-Reflex 2	глубокомат.	2	86	10,0 м²
	пол		**KM1**	по образцу	Coswick · Вековые традиции · арт. 1167-4250				10,0 м²
	плинтус		**K7**	Farrow & Ball No. 15	Orac Decor · Contour (Luxxus)			53	12,0 м
7. Ванная 8,44 м²	стены		**KM3**	Marvel Travertine	Atlas Concorde · арт. A8UZ				28,8 м²
	потолок		**K8**	Tikkurila V503	Tikkurila · Luja 7	матовая	1	86	8,4 м²
	пол		**KM4**	по образцу	керамогранит · аналог по хар.				8,4 м²
8. Прихожая 7,89 м²	стены		**K1**	Farrow & Ball No. 15	Farrow & Ball · Modern Emulsion	матовая	1	53	20,4 м²
	потолок		**K3**	Tikkurila V503	Tikkurila · Anti-Reflex 2	глубокомат.	2	86	7,9 м²
	пол		**KM5**	Marvel Travertine	Atlas Concorde · арт. A8UZ				7,9 м²
	плинтус		**K4**	Farrow & Ball No. 15	МДФ · в цвет Farrow & Ball			53	7,0 м
9. Санузел гостевой 4,49 м²	стены		**KM3**	Marvel Travertine	Atlas Concorde · арт. A8UZ				21,4 м²
	потолок		**K8**	Tikkurila V503	Tikkurila · Luja 7	матовая	1	86	4,5 м²
	пол		**KM4**	по образцу	керамогранит · аналог по хар.				4,5 м²

Примечания

1. Цвет на листе и на экране — ориентир. До покраски — выкрас на объекте: не меньше А3 (или лист ГКЛ), на грунте под эту краску, не на белой шпаклёвке, в 2 слоя; на обороте — код, бренд, веер, дата. Смотреть днём и вечером, рядом с образцами пола и плитки; к основному цвету стен — ещё 2 соседних оттенка. Красить только в цвет утверждённого выкраса.
2. Краску заказывать по коду из графы «Система и код цвета» у бренда этого кода, не «аналогом» другого; весь объём одного кода — одной партией, колеруемую краску — за один проход машины.
3. Площади — те же, что в ведомости отделки (лист С1); сколько краски заказать — в спецификации отделочных материалов (лист С3).

Схема палитры проекта

Стиль: Модерн (ар-нуво) 60% + Современный (контемпорари) 40% · схема: аналоговая

основной	основной	второстепенный	второстепенный	акцентный	акцентный	акцентный
Farrow & Ball No. 15	**Tikkurila V503**	**Farrow & Ball No. 34**	**Farrow & Ball No. 286**	**NCS S 5030-B10G**	**Farrow & Ball No. 66**	**NCS S 8010-Y30R**
Bone — мягкий каменно-серый с зеленцой LRV 53 стены 1,3,4,5,6,8; плинтус 1,3,4,5,6,8	Winter LRV 86 потолок 1,2,3,4,5,6,7,8,9; стены 2; плинтус 2; текстиль/декор 1,3,4,6	Calke Green — традиционный шалфей LRV 22 акцент 1,3,4,6; текстиль/декор 1,3,4,6	Peignoir — серо-розовый LRV 57 текстиль/декор 3,6	Павлиний сине-зелёный LRV 12 текстиль/декор 3,6	India Yellow — глубокая горчица LRV 36 текстиль/декор 3,4,6	Тёмно-коричневый LRV 3 в отделке не применён

План 60/30/10



Окраска, факт — по площади стен, акцентов, потолков



окрашено всего 364 м²; второстепенный тон несут мебель и текстиль

Текстиль и декор в цветах вне палитры проекта

- NCS S 2010-Y30R Тёплый льняной беж — пом. 1 (T1, T27, T4), 3 (T7), 4 (T13, T17), 6 (T20)
- NCS S 5020-G50Y Оливковый — пом. 1 (T3)

Условные обозначения

- **K1** Farrow & Ball No. 15 · Bone — мягкий каменно-серый с зеленцой · Modern Emulsion · матовая · кл. 1
- **K2** Farrow & Ball No. 34 · Calke Green — традиционный шалфей · Modern Emulsion · матовая · кл. 1
- **K3** Tikkurila V503 · Winter · Anti-Reflex 2 · глубокомат. · кл. 2
- **K4** Farrow & Ball No. 15 · Bone — мягкий каменно-серый с зеленцой · МДФ
- **K5** Tikkurila V503 · Winter · Harmony · матовая · кл. 1
- **K6** Tikkurila V503 · Winter · МДФ
- **K7** Farrow & Ball No. 15 · Bone — мягкий каменно-серый с зеленцой · Contour (Luxxus)
- **K8** Tikkurila V503 · Winter · Luja 7 · матовая · кл. 1
- дерево (доска, паркет, ламинат) — рисунок досок
- керамогранит, плитка, камень — сетка швов по формату
- **KM1** инженерная доска · 1167-4250
- **KM2** аналог: керамогранит под травертин, матовый, 1200×600×9 мм
- **KM3** плитка · A8UZ
- **KM4** аналог: керамогранит ректифицированный под травертин, матовый, 600×600×9 мм
- **KM5** керамогранит · A8UZ

К — краска, КМ — отделочный материал (тон КМ — по описанию, эталон — образец материала); кл. — класс истирания (1 — самый стойкий к мытью); LRV — светлота цвета: 0 — чёрный, 100 — белый


Перечень выкрасов на согласование

№	Код	Бренд / веер	Пом. / стена	Подложка	Формат	Статус
1	No. 15	Farrow & Ball	1, 3, 4, 5, 6, 8	ГКЛ с грунтом; МДФ под эмаль	600×1000; 300×600	к выполнению
2	No. 34	Farrow & Ball	1 A, 3 A, 4 A, 6 A	ГКЛ с грунтом	600×1000	к выполнению
3	V503	Tikkurila	1, 2, 3, 4, 5, 6, 7, 8, 9	ГКЛ с грунтом; МДФ под эмаль	600×1000; 300×600	к выполнению

	Лист	№ док.	Подпись	Дата	Проект: Квартира с кабинетом
Дизайнер	Кырлан А.С.			04.11.26	Колерная карта

Стадия	Лист	Листов
П	36	127

выпуск 04.11.2026 № 627e1ac6ce · стр. 36 из 127

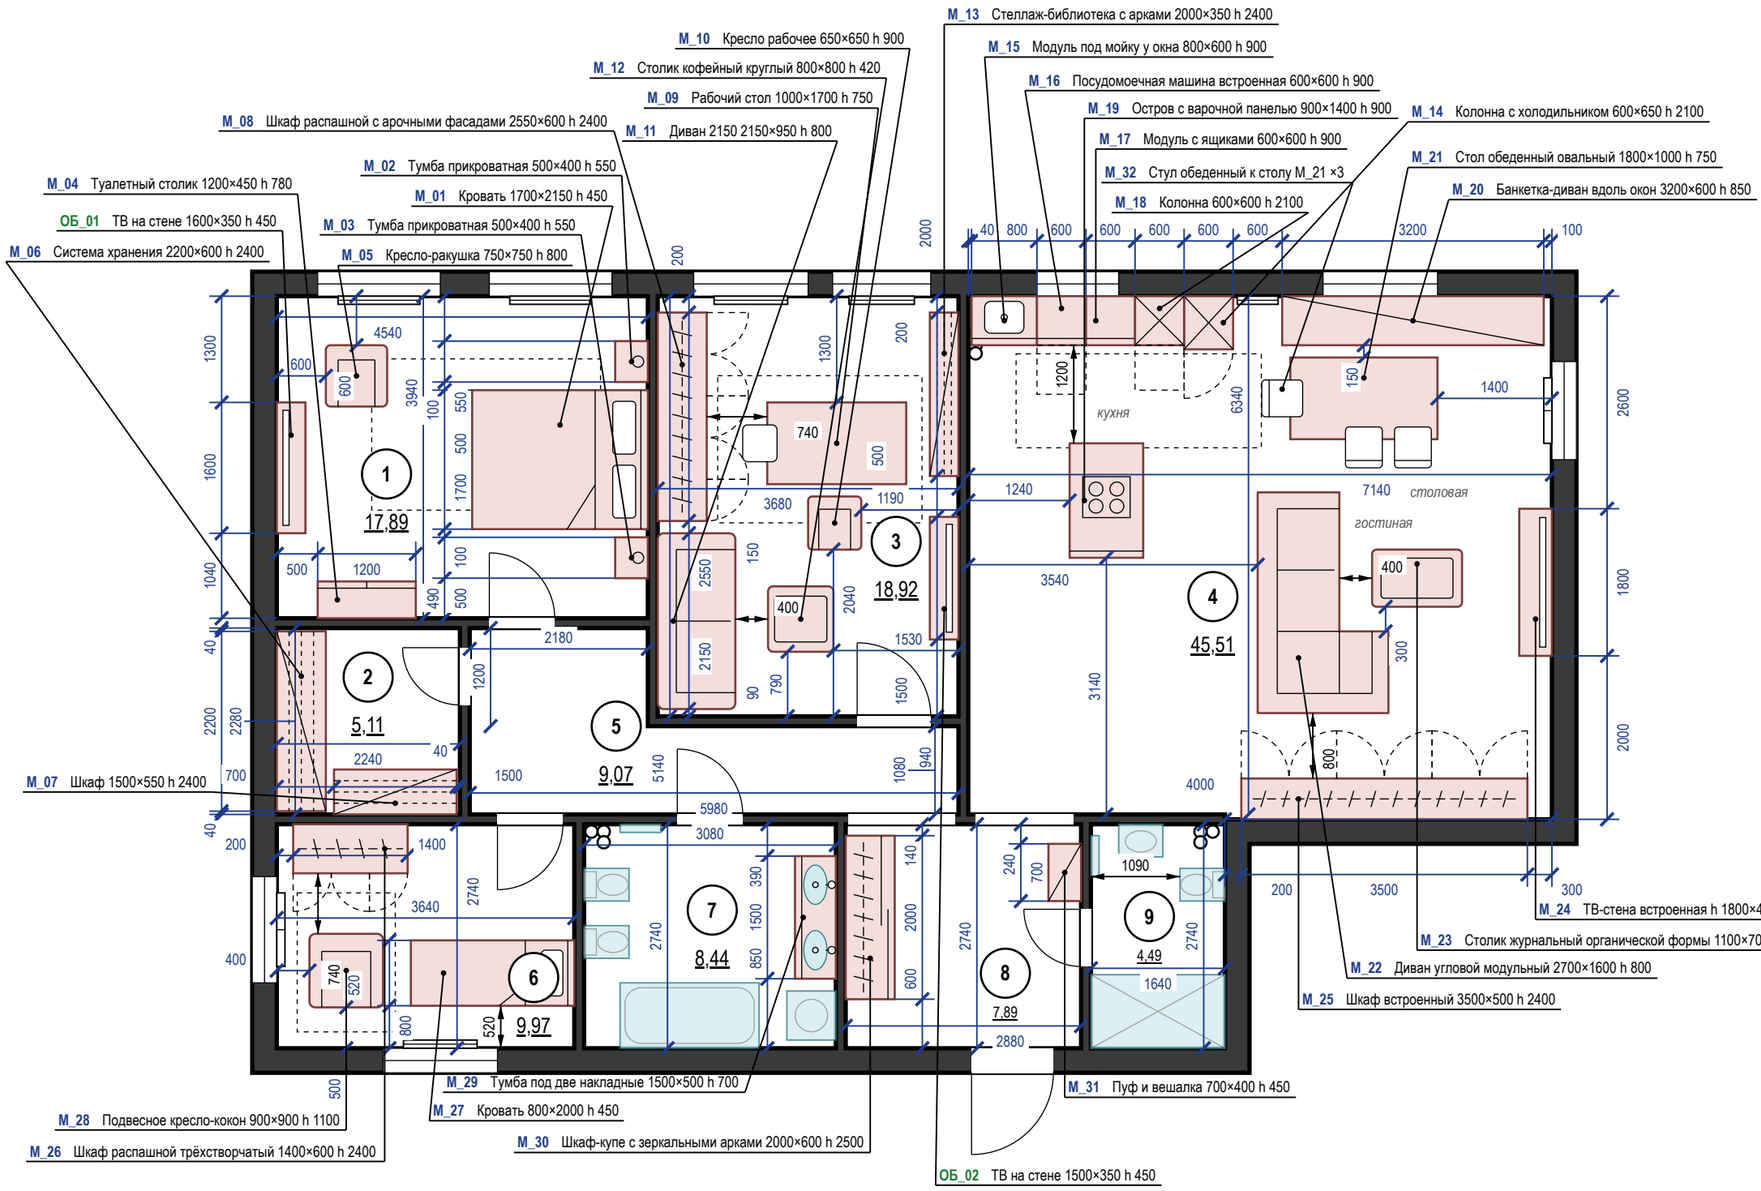

Экспликация помещений

лист 30 · на плане — номера в марках

Ведомость мебели и оборудования

Марка	Наименование	Ш×Г×В, мм	Пом.	Кол.
M_01	Кровать 1700×2150	1700×2150×450	1	1
M_02	Тумба прикроватная	500×400×550	1	1
M_03	Тумба прикроватная	500×400×550	1	1
ОБ_01	ТВ на стене	1600×350×450	1	1
M_04	Туалетный столик	1200×450×780	1	1
M_05	Кресло-ракушка	750×750×800	1	1
M_06	Система хранения	2200×600×2400	2	1
M_07	Шкаф	1500×550×2400	2	1
M_08	Шкаф распашной с арочными фасадами	2550×600×2400	3	1
M_09	Рабочий стол 1700×1000	1000×1700×750	3	1
M_10	Кресло рабочее	650×650×900	3	1
M_11	Диван 2150	2150×950×800	3	1
M_12	Столик кофейный круглый	800×800×420	3	1
M_13	Стеллаж-библиотека с арками	2000×350×2400	3	1
ОБ_02	ТВ на стене	1500×350×450	3	1
M_14	Колонна с холодильником	600×650×2100	4	1
M_15	Модуль под мойку у окна	800×600×900	4	1
M_16	Посудомоечная машина встроенная	600×600×900	4	1
M_17	Модуль с ящиками	600×600×900	4	1
M_18	Колонна	600×600×2100	4	1
M_19	Остров 900×1400 с варочной панелью	900×1400×900	4	1
M_20	Банкетка-диван вдоль окон	3200×600×850	4	1
M_21	Стол обеденный овальный 1800×1000	1800×1000×750	4	1
M_22	Диван угловой модульный	2700×1600×800	4	1
M_23	Столик журнальный органической формы	1100×700×380	4	1
M_24	ТВ-стена встроенная h 1800×400 h	1800×400×2500	4	1
M_25	Шкаф встроенный	3500×500×2400	4	1
M_26	Шкаф распашной трёхстворчатый	1400×600×2400	6	1
M_27	Кровать 800×2000	800×2000×450	6	1
M_28	Подвесное кресло-кокон	900×900×1100	6	1
M_29	Тумба под две накладные	1500×500×700	7	1
M_30	Шкаф-купе с зеркальными арками	2000×600×2500	8	1
M_31	Пуф и вешалка	700×400×450	8	1
M_32	Стул обеденный к столу M_21	450×500×820	4	3

Ш — вдоль стены (изголовья), Г — от стены (длина кровати)

Материалы, модели, допуск замены — лист 38

Примечания

1. Размеры — в мм от чистовых поверхностей стен; размеры мебели уточнить после отделочных работ; общие указания — лист 27.
2. Стулья обеденной группы (M_32 — 3 шт.) показаны в рабочем положении, задвинутыми под столешницу на 150 мм.

					Проект: Квартира с кабинетом	M 1:75
	Лист	№ док.	Подпись	Дата		
Дизайнер	Кырлан А.С.			04.11.26	План размещения мебели и оборудования	Стадия: П; Лист: 37; Листов: 127

Поз.	Наименование и техническая характеристика	Тип, марка, обозначение документа, опросного листа	Код продукции	Поставщик	Ед. измерения	Кол.	Масса 1 ед., кг	Примечание
	Мебель встроенная и корпусная (изготовление по чертежам мебельщика)							
M_06	Система хранения: штанги, полки, ящики; каркас и полки — ЛДСП 16 мм, декор «дуб натуральный»; без фасадов; Ш×Г×В 2200×600×2400 мм			изготовление на заказ	шт.	1		пом. 2; крепление к стене
M_07	Шкаф с выдвижной гладильной доской и полками; каркас и полки — ЛДСП 16 мм, декор «дуб натуральный»; без фасадов; Ш×Г×В 1500×550×2400 мм			изготовление на заказ	шт.	1		пом. 2; крепление к стене
M_08	Шкаф распашной с арочными фасадами; корпус ЛДСП 16 мм; фасады — МДФ 18 мм, эмаль матовая; арочная фрезеровка филёнки (полукруглый верх, поле 100 мм); Ш×Г×В 2550×600×2400 мм			изготовление на заказ	шт.	1		пом. 3
M_14	Колонна с холодильником; корпус ЛДСП 16 мм; фасады — МДФ 18 мм, эмаль матовая; цвет фасадов — в цвет стен (Farrow & Ball No. 15); Ш×Г×В 600×650×2100 мм			изготовление на заказ	шт.	1		пом. 4
M_15	Модуль под мойку у окна; корпус ЛДСП 16 мм; фасады — МДФ 18 мм, эмаль матовая; цвет фасадов — в цвет стен (Farrow & Ball No. 15); Ш×Г×В 800×600×900 мм			изготовление на заказ	шт.	1		пом. 4
M_16	Модуль под встраиваемую ПММ 60; без корпуса (ниша между соседними модулями); фасад на дверь машины — МДФ 18 мм, эмаль матовая; цоколь; цвет фасадов — в цвет стен (Farrow & Ball No. 15); Ш×Г×В 600×600×900 мм			изготовление на заказ	шт.	1		пом. 4
M_17	Модуль с ящиками; корпус ЛДСП 16 мм; фасады — МДФ 18 мм, эмаль матовая; цвет фасадов — в цвет стен (Farrow & Ball No. 15); Ш×Г×В 600×600×900 мм			изготовление на заказ	шт.	1		пом. 4
M_18	Колонна: духовой шкаф и СВЧ; корпус ЛДСП 16 мм; фасады — МДФ 18 мм, эмаль матовая; цвет фасадов — в цвет стен (Farrow & Ball No. 15); Ш×Г×В 600×600×2100 мм			изготовление на заказ	шт.	1		пом. 4
M_19	Остров 900×1400 с варочной панелью, столешница — травертин; корпус ЛДСП 16 мм; фасады — МДФ 18 мм, эмаль матовая; цвет фасадов — в цвет стен (Farrow & Ball No. 15); Ш×Г×В 900×1400×900 мм			изготовление на заказ	шт.	1		пом. 4
M_20	Банкетка-диван вдоль окон, бархат — экран радиатора, изготовление на заказ; Ш×Г×В 3200×600×850 мм			изготовление на заказ	шт.	1		пом. 4
M_24	ТВ-стена встроенная 1800×400 h 2500: каркас на стене Б, панели МДФ с волнистым рельефом (эмаль), ниша ТВ 1500×900 на отметке +900 (низ), ниша биокамина 900×400 на отметке +350 (низ), облицовка ниши камина — негорючая (сталь / камень), вентиляционные зазоры 50 мм над топкой; корпус оцинкованный профиль ПП 60×27 / ПН 28×27 (НГ), на стене Б 27 мм; фасады — панели МДФ 19 мм с волнистым рельефом, эмаль матовая; Ш×Г×В 1800×400×2500 мм			изготовление на заказ	шт.	1		пом. 4
M_25	Шкаф встроенный, фасады с округлыми торцами; корпус ЛДСП 16 мм; фасады — МДФ 18 мм, эмаль матовая; цвет фасадов — в цвет стен (Farrow & Ball No. 15); Ш×Г×В 3500×500×2400 мм			изготовление на заказ	шт.	1		пом. 4
M_26	Шкаф распашной трёхстворчатый с антресолью; корпус ЛДСП 16 мм; фасады — МДФ 18 мм, эмаль матовая; цвет фасадов в цвет стен (Farrow & Ball No. 15); Ш×Г×В 1400×600×2400 мм			изготовление на заказ	шт.	1		пом. 6; крепление к стене
M_29	Тумба под две накладные раковины C_02, C_03, 1500 мм, напольная; корпус ЛДСП 16 мм; фасады — МДФ 18 мм, эмаль матовая; цвет фасадов — в цвет стен (Atlas Concorde A8UZ); Ш×Г×В 1500×500×700 мм			изготовление на заказ	шт.	1		пом. 7; крепление к стене
M_30	Шкаф-купе с зеркальными арками; корпус ЛДСП 16 мм; фасады — МДФ 10 мм, эмаль матовая в профиле: алюминий, латунь матовая; вставка — зеркало серебро 4 мм, плёнка безопасности, арочная (полукруглый верх, поле 100 мм); Ш×Г×В 2000×600×2500 мм			изготовление на заказ	шт.	1		пом. 8
	Мебель покупная							
M_01	Кровать 1700×2150 с высоким округлым изголовьем, бархат; мягкое изголовье, обивка — ткань, цвет Farrow & Ball No. 34; Ш×Г×В 1700×2150×450 мм			аналог по характеристикам	шт.	1		пом. 1; замена ≤ габарита
M_02, M_03	Тумба прикроватная, морёный дуб, латунные ручки; шпон, дуб натуральный, матовое масло; Ш×Г×В 500×400×550 мм			аналог по характеристикам	шт.	2		пом. 1; замена ≤ габарита
M_04	Туалетный столик с овальным зеркалом в латунной раме; шпон, дуб натуральный, матовое масло; Ш×Г×В 1200×450×780 мм			аналог по характеристикам	шт.	1		пом. 1; замена ≤ габарита
M_05	Кресло-ракушка, бархат павлиньего цвета; обивка — ткань, цвет Farrow & Ball No. 34; Ш×Г×В 750×750×800 мм			аналог по характеристикам	шт.	1		пом. 1; замена ≤ габарита
ОБ_01	ТВ на стене, тумба подвесная с волнистым фасадом; шпон, дуб натуральный, матовое масло; Ш×Г×В 1600×350×450 мм			аналог по характеристикам	шт.	1		пом. 1; замена ≤ габарита
M_09	Рабочий стол 1700×1000, морёный дуб, округлые углы; шпон, дуб натуральный, матовое масло; Ш×Г×В 1000×1700×750 мм			аналог по характеристикам	шт.	1		пом. 3; замена ≤ габарита

Примечания

1. Позиции мебели совпадают с марками на плане расстановки; размеры Ш×Г×В — Ш вдоль стены, Г от стены.
2. Размеры и привязки плана расстановки — в мм от чистовых поверхностей стен: слой штукатурки 20 мм по блоку и 5 мм шпаклёвки по ГКЛ учтён; привязки — от стен и углов помещения, а не от другой мебели.
3. План расстановки не является документацией для изготовления мебели. Встроенная и корпусная мебель изготавливается по чертежам мебельщика после контрольного обмера (после штукатурки); «стена в стену» — с зазором 10 мм с каждой стороны или с компенсаторами; графы «Тип, марка» и «Код продукции» для неё не заполняются (ГОСТ 21.110-2013).
4. Покупные изделия — аналог по характеристикам: заменять только на изделия не больше указанного габарита и того же материала и цвета.
5. Материал и цвет, не указанные в данных изделия, приняты по концепции: тон дерева — по полу, обивка — по вторичному цвету палитры; образцы согласовать до заказа.
6. Масса 1 ед. для изделий до 25 кг не указывается. Техника — по монтажным схемам изготовителя; выводы — по листам ЭОМ и ВК.

					Проект: Квартира с кабинетом
	Лист	№ док.	Подпись	Дата	Спецификация мебели и оборудования
Дизайнер	Кырлан А.С.			04.11.26	Стадия: П; Лист: 38; Листов: 127

Поз.	Наименование и техническая характеристика	Тип, марка, обозначение документа, опросного листа	Код продукции	Поставщик	Ед. измерения	Кол.	Масса 1 ед., кг	Примечание
M_10	Кресло рабочее, кожа карамельного цвета; обивка — ткань, цвет Farrow & Ball No. 34; Ш×Г×В 650×650×900 мм			аналог по характеристикам	шт.	1		пом. 3; замена ≤ габарита
M_11	Диван 2150 с мягкими округлыми подлокотниками; обивка — ткань, цвет Farrow & Ball No. 34; Ш×Г×В 2150×950×800 мм			аналог по характеристикам	шт.	1		пом. 3; замена ≤ габарита
M_12	Столик кофейный круглый, травертин; шпон, дуб натуральный, матовое масло; Ш×Г×В 800×800×420 мм			аналог по характеристикам	шт.	1		пом. 3; замена ≤ габарита
M_13	Стеллаж-библиотека с арками; шпон, дуб натуральный, матовое масло; Ш×Г×В 2000×350×2400 мм			аналог по характеристикам	шт.	1		пом. 3; замена ≤ габарита
ОБ_02	ТВ на стене, тумба подвесная; шпон, дуб натуральный, матовое масло; Ш×Г×В 1500×350×450 мм			аналог по характеристикам	шт.	1		пом. 3; замена ≤ габарита
M_21	Стол обеденный овальный 1800×1000, морёный дуб; шпон, дуб натуральный, матовое масло; Ш×Г×В 1800×1000×750 мм			аналог по характеристикам	шт.	1		пом. 4; замена ≤ габарита
M_22	Диван угловой модульный с округлыми формами, бархат павлиньего цвета; Г-образный: основная секция 2700, вторая 1000 × 1600 мм; обивка — ткань, цвет Farrow & Ball No. 34; Ш×Г×В 2700×1600×800 мм			аналог по характеристикам	шт.	1		пом. 4; замена ≤ габарита
M_23	Столик журнальный органической формы, травертин; шпон, дуб натуральный, матовое масло; Ш×Г×В 1100×700×380 мм			аналог по характеристикам	шт.	1		пом. 4; замена ≤ габарита
M_32	Стул обеденный к столу M_21; обивка — ткань, цвет Farrow & Ball No. 34; каркас — дуб натуральный; Ш×Г×В 450×500×820 мм			аналог по характеристикам	шт.	3		пом. 4; замена ≤ габарита
M_27	Кровать 800×2000 с мягким изголовьем-облаком; мягкое изголовье, обивка — ткань, цвет Farrow & Ball No. 34; Ш×Г×В 800×2000×450 мм			аналог по характеристикам	шт.	1		пом. 6; замена ≤ габарита
M_28	Подвесное кресло-кокон; обивка — ткань, цвет Farrow & Ball No. 34; Ш×Г×В 900×900×1100 мм			аналог по характеристикам	шт.	1		пом. 6; замена ≤ габарита
M_31	Пуф и вешалка; Ш×Г×В 700×400×450 мм			аналог по характеристикам	шт.	1		пом. 8; замена ≤ габарита
	Техника встраиваемая и бытовая (покупные изделия), светильники под розетки							
	Холодильник встраиваемый, в модуле M_14	аналог по характеристикам: полновстраиваемый под фасад, ниша 1780 × 560 × 550 мм, вентиляция решётка в цоколе, выход сверху		по выбору заказчика до изготовления мебели	шт.	1		пом. 4; по схеме изготовителя
	Посудомоечная машина встраиваемая, в модуле M_16; ниша 600 мм	аналог по характеристикам: полновстраиваемая 60 см под фасад, ниша 600 × 862 мм, навеска фасада в комплекте		по выбору заказчика до изготовления мебели	шт.	1		пом. 4; по схеме изготовителя
	Духовой шкаф встраиваемый, в модуле M_18	аналог по характеристикам: 60 см, лицевая панель 595 мм, ниша 568 × 600, глубина ≥ 550 мм, вентиляция за прибором		по выбору заказчика до изготовления мебели	шт.	1		пом. 4; по схеме изготовителя
	СВЧ-печь встраиваемая, в модуле M_18	аналог по характеристикам: встраиваемая 38 см, лицевая панель 388 мм, ниша 568 × 380, глубина ≥ 550 мм		по выбору заказчика до изготовления мебели	шт.	1		пом. 4; по схеме изготовителя
	Вытяжка, над островом M_19, потолочная, 900 мм, рециркуляция (угольный фильтр), низ +1,550	аналог по характеристикам: производительность — по расчёту ОВ, шум ≤ 55 дБ(А)		по выбору заказчика до изготовления мебели	шт.	1		пом. 4; по схеме изготовителя
	Варочная панель встраиваемая, индукционная, в модуле M_19	аналог по характеристикам: индукционная 60 см, вырез 560 × 490 мм по шаблону модели		по выбору заказчика до изготовления мебели	шт.	1		пом. 4; по схеме изготовителя
	Стиральная машина, место по листу ВК (ОБ_03); Ш×Г 600×600 мм	аналог по характеристикам: тип загрузки — по листу ВК, в плане 600 × 600 мм (ширина × глубина), по листу ВК		по выбору заказчика до изготовления мебели	шт.	1		пом. 7; по схеме изготовителя
	Торшер, у поз. ОБ_01; абажур — ткань или опаловое стекло; лампа 2700 K			аналог по характеристикам	шт.	1		пом. 1; розетка P5 (ЭОМ)
	Текстиль							
T1	Портьеры-волна; лён 100 %; цвет NCS S 2010-Y30R; карниз 2300 мм, высота 2590 мм, сборка 2			аналог по характеристикам	шт.	2		пом. 1
T2	Тюль; полиэстер 100 %; цвет Tikkurila V503; карниз 2300 мм, высота 2590 мм, сборка 2,5			аналог по характеристикам	шт.	1		пом. 1
T27	Портьеры-волна; лён 100 %; цвет NCS S 2010-Y30R; карниз 2300 мм, высота 2590 мм, сборка 2			аналог по характеристикам	шт.	2		пом. 1
T28	Тюль; полиэстер 100 %; цвет Tikkurila V503; карниз 2300 мм, высота 2590 мм, сборка 2,5			аналог по характеристикам	шт.	1		пом. 1
T3	Ковёр под кроватью; шерсть 80 %, хлопок 20 %; цвет NCS S 5020-G50Y; 2800×1850 мм			аналог по характеристикам	шт.	1		пом. 1; с подложкой
T4	Подушки декоративные на кровать; лён 100 %; цвет NCS S 2010-Y30R			аналог по характеристикам	шт.	3		пом. 1
T5	Подушки на кровать, акцент; хлопковый бархат 100 %; цвет Farrow & Ball No. 34			аналог по характеристикам	шт.	2		пом. 1
T6	Плед на кровать; шерсть мериноса 100 %; цвет Farrow & Ball No. 34			аналог по характеристикам	шт.	1		пом. 1

					Проект: Квартира с кабинетом
	Лист	№ док.	Подпись	Дата	
Дизайнер	Кырлан А.С.			04.11.26	Спецификация мебели и оборудования (продолжение)

Стадия	Лист	Листов
П	39	127

Поз.	Наименование и техническая характеристика	Тип, марка, обозначение документа, опросного листа	Код продукции	Поставщик	Ед. измерения	Кол.	Масса 1 ед., кг	Примечание
Т7	Портьеры-волна; лён 100 %; цвет NCS S 2010-Y30R; карниз 1820 мм, высота 2590 мм, сборка 2			аналог по характеристикам	шт.	2		пом. 3
Т8	Тюль; полиэстер 100 %; цвет Tikkurila V503; карниз 1820 мм, высота 2590 мм, сборка 2,5			аналог по характеристикам	шт.	1		пом. 3
Т9	Ковёр под кроватью; шерсть 100 %; цвет Farrow & Ball No. 66; 2500×1800 мм			аналог по характеристикам	шт.	1		пом. 3; с подложкой
Т10	Подушки декоративные на кровать; букле (шерсть 60 %, полиэстер 40 %); цвет Farrow & Ball No. 286			аналог по характеристикам	шт.	3		пом. 3
Т11	Подушки на кровать, акцент; хлопковый бархат 100 %; цвет NCS S 5030-B10G			аналог по характеристикам	шт.	2		пом. 3
Т12	Плед на кровать; шерсть мериноса 100 %; цвет Farrow & Ball No. 34			аналог по характеристикам	шт.	1		пом. 3
Т13	Портьеры-волна (гостиная); лён 70 %, вискоза 30 %; цвет NCS S 2010-Y30R; карниз 1650 мм, высота 2690 мм, сборка 2			аналог по характеристикам	шт.	2		пом. 4
Т14	Тюль (гостиная); полиэстер 100 %; цвет Tikkurila V503; карниз 1650 мм, высота 2690 мм, сборка 2,5			аналог по характеристикам	шт.	1		пом. 4
Т15	Римская штора (кухня); лён 100 %; цвет Farrow & Ball No. 66; карниз 1400 мм, высота 1700 мм			аналог по характеристикам	шт.	1		пом. 4
Т26	Римская штора (кухня, окно над рабочей зоной); лён 100 %; цвет Farrow & Ball No. 66; карниз 1000 мм, высота 1700 мм			аналог по характеристикам	шт.	1		пом. 4
Т16	Ковёр в зоне отдыха; шерсть 100 %; цвет Farrow & Ball No. 66; 3000×1150 мм			аналог по характеристикам	шт.	1		пом. 4; с подложкой
Т17	Подушки на диван; букле (шерсть 60 %, полиэстер 40 %); цвет NCS S 2010-Y30R			аналог по характеристикам	шт.	3		пом. 4
Т18	Подушки на диван, акцент; хлопковый бархат 100 %; цвет Farrow & Ball No. 34			аналог по характеристикам	шт.	2		пом. 4
Т19	Плед на диван; альпака 50 %, шерсть 50 %; цвет Farrow & Ball No. 66			аналог по характеристикам	шт.	1		пом. 4
Т20	Портьеры-волна; лён 100 %; цвет NCS S 2010-Y30R; карниз 1820 мм, высота 2590 мм, сборка 2			аналог по характеристикам	шт.	2		пом. 6
Т21	Тюль; полиэстер 100 %; цвет Tikkurila V503; карниз 1820 мм, высота 2590 мм, сборка 2,5			аналог по характеристикам	шт.	1		пом. 6
Т22	Ковёр у кресла-кокона (зона чтения); шерсть 100 %; цвет Farrow & Ball No. 66; 1200×1700 мм			аналог по характеристикам	шт.	1		пом. 6; с подложкой
Т23	Подушки декоративные на кровать; букле (шерсть 60 %, полиэстер 40 %); цвет Farrow & Ball No. 286			аналог по характеристикам	шт.	3		пом. 6
Т24	Подушки на кровать, акцент; хлопковый бархат 100 %; цвет NCS S 5030-B10G			аналог по характеристикам	шт.	2		пом. 6
Т25	Плед на кровать; шерсть мериноса 100 %; цвет Farrow & Ball No. 34			аналог по характеристикам	шт.	1		пом. 6
	Декор							
ДК1	Картина над кроватью: абстракция, холст, тонкая рама из дуба; 1200×700 мм; низ на 1300 мм от пола			аналог по характеристикам	шт.	1	4	пом. 1; крепление к стене
ДК3	Картина над диваном: графика в паспарту, рама — дуб; 1400×700 мм; низ на 1000 мм от пола			аналог по характеристикам	шт.	1	4	пом. 3; крепление к стене
ДК4	Зеркало в рост в тонкой чёрной раме; рама — чёрный матовый; 600×1600 мм; низ на 300 мм от пола			аналог по характеристикам	шт.	1	12	пом. 3; крепление: анкер для пустотелых оснований, 4 шт.
ДК6	Картина: крупная абстракция в тёплой гамме, холст на подрамнике; 1200×900 мм; центр на 1550 мм от пола			аналог по характеристикам	шт.	1	6	пом. 4; крепление: анкер, 2 шт.
ДК7	Растение в кашпо; 450×450 мм			аналог по характеристикам	шт.	1		пом. 4
ДК8	Ваза керамическая с ветками на обеденном столе; 200×350 мм; на M_21			аналог по характеристикам	шт.	1		пом. 4
ДК2	Картина над кроватью: графика в паспарту, рама — дуб; 600×700 мм; низ на 1200 мм от пола			аналог по характеристикам	шт.	1	4	пом. 6; крепление к стене
ДК5	Зеркало в рост в тонкой чёрной раме; рама — чёрный матовый; 600×1600 мм; низ на 300 мм от пола			аналог по характеристикам	шт.	1	12	пом. 6; крепление: анкер для пустотелых оснований, 4 шт.
ДК10	Зеркало над умывальниками, влагостойкое, в тонкой латунной раме; 1400×700 мм; низ на 1200 мм от пола			аналог по характеристикам	шт.	1	12	пом. 7; крепление: клей для зеркал + 2 опорных уголка снизу, анкеры по основанию
ДК9	Зеркало; рама — чёрный матовый; 800×1800 мм; низ на 550 мм от пола			аналог по характеристикам	шт.	1	18	пом. 8; крепление: анкер, 4 шт.
ДК11	Зеркало над умывальником, влагостойкое, в тонкой латунной раме; 500×700 мм; низ на 1200 мм от пола			аналог по характеристикам	шт.	1	5	пом. 9; крепление: клей для зеркал + 2 опорных уголка снизу

					Проект: Квартира с кабинетом		
	Лист	№ док.	Подпись	Дата	Спецификация мебели и оборудования (продолжение)	Стадия	Лист	Листов
Дизайнер	Кырлан А.С.			04.11.26		П	40	127

Ведомость изделий

Марка	Наименование	Пом.	Ш×Г×В, мм	Корпус	Фасад	Кромка, мм	Кол.
M_06	Система хранения	2	2200×600×2400	ЛДСП 16	без фасадов	0,4 / 2	1
M_07	Система хранения	2	1500×550×2400	ЛДСП 16	без фасадов	0,4 / 2	1
M_08	Шкаф распашной	3	2550×600×2400	ЛДСП 16	МДФ 18 мм, эмаль матовая; арочная фрезеровка филёнки (полукруглый верх, поле 100 мм)	0,4 / 2	1
M_24	ТВ-стена	4	1800×400×2500	оцинкованный профиль ПП 60×27 / ПН 28×27 (НГ), на стене Б	панели МДФ 19 мм с волнистым рельефом, эмаль матовая	0,4 / 2	1
M_25	Шкаф распашной	4	3500×500×2400	ЛДСП 16	МДФ 18 мм, эмаль матовая	0,4 / 2	1
M_26	Шкаф распашной	6	1400×600×2400	ЛДСП 16	МДФ 18 мм, эмаль матовая	0,4 / 2	1
M_29	Тумба под раковину	7	1500×500×700	ЛДСП 16	МДФ 18 мм, эмаль матовая	0,4 / 2	1
M_30	Шкаф-купе	8	2000×600×2500	ЛДСП 16	МДФ 10 мм, эмаль матовая в профиле: алюминий, латунь матовая; вставка — зеркало серебро 4 мм, плёнка безопасности, арочная (полукруглый верх, поле 100 мм)	0,4 / 2	1
M_15	Модуль нижний: мойка	4	800×600×900	ЛДСП 16	МДФ 18 мм, эмаль матовая	0,4 / 2	1
M_16	Модуль под ПММ 60: без корпуса, фасад на дверь машины	4	600×600×900	без корпуса	МДФ 18 мм, эмаль матовая — на дверь машины (навеска из её комплекта), цоколь		1
M_17	Модуль нижний: ящики	4	600×600×900	ЛДСП 16	МДФ 18 мм, эмаль матовая	0,4 / 2	1
M_18	Пенал: духовой шкаф, СВЧ	4	600×600×2100	ЛДСП 16	МДФ 18 мм, эмаль матовая	0,4 / 2	1
M_14	Пенал: холодильник встр.	4	600×650×2100	ЛДСП 16	МДФ 18 мм, эмаль матовая	0,4 / 2	1
M_19	Остров (M_19.1, M_19.2, M_19.3)	4	1400×900×900	ЛДСП 16	МДФ 18 мм, эмаль матовая	0,4 / 2	1
M_20	банкетка-диван вдоль окон, бархат — экран радиатора, изготовление на заказ РО-6: решётка в лицевой панели, щель 60, зазор 50	4	3200×600×850	по чертежу	решётка по ширине прибора	0,4 / 2	1

Ведомость встраиваемой техники

Поз.	Прибор	Ниша, вырез, мм	Вентиляция	Питание	Схема
M_15	Мойка врезная / подстольная с сифоном	вырез по шаблону, ориентир 700 × 480		смеситель — выводы ВК	по модели
M_16	Посудомоечная машина встраиваемая, 60 см	ниша 600 × 862 (от пола до низа столешницы)	зазор в цоколе, по схеме	Р32: M_17, H=300 — в соседнем модуле, за ящиком	по модели
M_18	Духовой шкаф встраиваемый, 60 см	ниша 568 × 600, глубина ≥ 550; низ +820	зазор 50 за прибором, без задней стенки; щель 50 в полке	ЭВ2: M_18, H=150 — за ящиком под нишей, доступ через ящик	по модели
M_18	СВЧ-печь встраиваемая, 38 см	ниша 568 × 380, глубина ≥ 550; низ +1436	зазор 50 за прибором, без задней стенки; щель 50 в полке	Р43: M_18, H=1960 — над нишами техники, за съёмной панелью антресоли	по модели
M_14	Холодильник встраиваемый, ниша 1780	ниша 1780 × 560 × 550	решётка в цоколе, канал за корпусом, выход сверху	Р25: M_14, H=2000 — над нишей холодильника, съёмная панель	по модели
M_19.2	Варочная панель индукционная, 60 см	вырез в столешнице 560 × 490, кромка выреза в 60 от рабочего края	зазор 40 мм под корпусом панели над верхним ящиком	ЭВ1: вывод из пола под островом, в цоколе, 700 мм от левого торца, 450 мм от рабочего края	по модели

Ведомость фурнитуры

№	Фурнитура	Тип, размер	Изделия	Кол.
1	Полкодержатель с фиксацией	ø5 мм	M_06, M_07, M_08, M_25, M_26, M_29, M_30, M_18, M_14, M_19	236
2	Штанга овальная 30×15, L = 712	+ 2 держателя	M_06	3
3	Опора регулируемая с цоколем на клипсах	ход 20 мм	M_06, M_07, M_08, M_25, M_26, M_29, M_30	56
4	Анкер по основанию стены	по таблице крепежа	M_06, M_07, M_08, M_24, M_25, M_26, M_29, M_30	52
5	Уголок крепления к стене от опрокидывания	стальной	M_06, M_07, M_08, M_24, M_25, M_26, M_29, M_30, M_18, M_14	20
6	Штанга овальная 30×15, L = 726	+ 2 держателя	M_07	1
7	Петля накладная 110° с доводчиком	чашка 35 мм	M_08, M_25, M_26, M_29, M_15, M_18, M_14	109
8	Штанга овальная 30×15, L = 996	+ 2 держателя	M_08	2
9	Штанга овальная 30×15, L = 486	+ 2 держателя	M_08	1
10	Штанга выдвижная торцевая	L по глубине	M_25	2
11	Штанга овальная 30×15, L = 909	+ 2 держателя	M_26	1
12	Система дверей купе: профиль, направляющие, ролики	на 3 двери	M_30	1
13	Ручка-профиль вертикальная	в цвет профиля	M_30	3
14	Штанга овальная 30×15, L = 653	+ 2 держателя	M_30	3
15	Полка для обуви выдвижная наклонная	ширина 630	M_30	2
16	Полка для обуви выдвижная наклонная	ширина 653	M_30	1
17	Ручка-профиль	латунь матовая	M_15, M_16, M_17, M_18, M_14, M_19	21
18	Опора кухонная регулируемая 100–120 мм	+ клипса цоколя	M_15, M_17, M_18, M_14, M_19	30
19	Комплект навески фасада ПММ	из поставки машины	M_16	1
20	Направляющие полного выдвижения с доводчиком NL 500	пара	M_17, M_18, M_19	14
21	Уголок крепления острова к полу	стальной, в цоколе	M_19	4


Примечания

1. Модели техники выбирает заказчик до изготовления мебели; ниши, вырезы и вентиляция — по монтажной схеме выбранной модели (условие гарантии), её номер вносится в ведомость.
2. Количество фурнитуры — по чертежам изделий; запас крепежа 5 %. Аналоги — по характеристикам (доводчик, нагрузка, ход).
3. Цвет корпусов, фасадов и профилей — по колерной карте проекта. Кромка — скрытые / видимые торцы, мм.


					Проект: Квартира с кабинетом
	Лист	№ док.	Подпись	Дата	
Дизайнер	Кырлан А.С.			04.11.26	Ведомости изделий, техники и фурнитуры

Стадия	Лист	Листов
П	41	127


Фрагмент 1. Ванная (пом. 7)

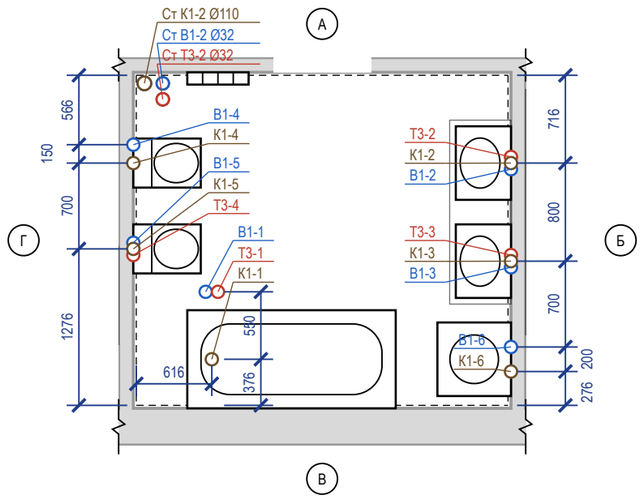

Фрагмент 2. Санузел гостевой (пом. 9)

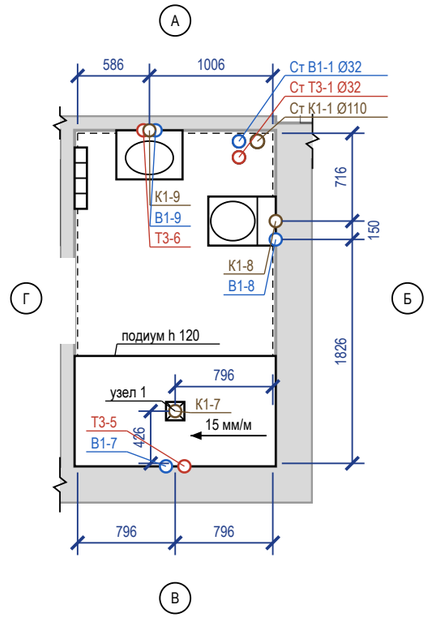

Фрагмент 3. Кухня-гостиная (пом. 4)

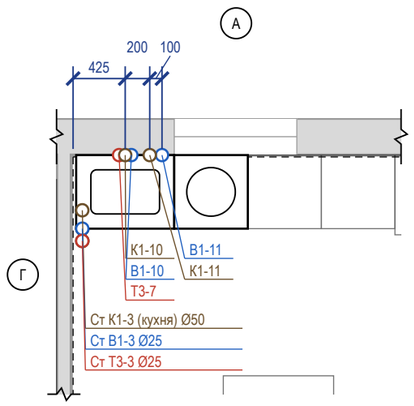

Условные обозначения

- вывод В1 (код — в ведомости привязок)
- вывод Т3 (код — в ведомости привязок)
- вывод К1 (код — в ведомости привязок)
- сантехприбор по расстановке (габарит модели)
- чистовая поверхность стены (от неё привязки)
- стояк «Ст К1-N / Ст В1-N» (ГОСТ 21.601), Ø мм
- линия обрыва (граница фрагмента)
- трап / лоток в полу
- направление уклона К1 / пола: Ø, мм на 1 м
- А — обозначение стены А–Г (как на развёртках)

Ведомость привязок выводов

Код	Прибор	Ø	H, мм	Привязка от чист. стен, мм	Прим.
В1-1	С_01 ванна	½"	0	566 от Г; 926 от В	в полу под стойку смесителя
Т3-1	С_01 ванна	½"	0	666 от Г; 926 от В	в полу под стойку смесителя
К1-1	С_01 ванна	Ø50	0	616 от Г; 376 от В	выпуск ванны в пол
В1-2	С_02 умывальник	½"	550	ст. Б: 766 от А	межос. 100
Т3-2	С_02 умывальник	½"	550	ст. Б: 666 от А	межос. 100
К1-2	С_02 умывальник	Ø50	500	ст. Б: 716 от А	
В1-3	С_03 умывальник	½"	550	ст. Б: 1126 от В	межос. 100
Т3-3	С_03 умывальник	½"	550	ст. Б: 1226 от В	межос. 100
К1-3	С_03 умывальник	Ø50	500	ст. Б: 1176 от В	
В1-4	С_04 унитаз подвесной	½"	1000	ст. Г: 566 от А	в раме инсталляции
К1-4	С_04 унитаз подвесной	Ø110	220	ст. Г: 716 от А	
В1-5	С_05 биде подвесное	½"	200	ст. Г: 1326 от В	межос. 100, в раме
Т3-4	С_05 биде подвесное	½"	200	ст. Г: 1226 от В	межос. 100, в раме
К1-5	С_05 биде подвесное	Ø50	200	ст. Г: 1276 от В	
В1-6	ОБ_03 стиральная машина	½"	800	ст. Б: 476 от В	кран машины
К1-6	ОБ_03 стиральная машина	Ø50	600	ст. Б: 276 от В	
В1-7	С_07 душ	½"	1220	ст. В: 721 от Г	межос. 150; 1100 от пола душа (подиум 120, +0,105)
Т3-5	С_07 душ	½"	1220	ст. В: 721 от Б	межос. 150; 1100 от пола душа (подиум 120, +0,105)
К1-7	С_07 душ	Ø50	120	796 от Б; 426 от В	трап в подиуме 120
В1-8	С_08 унитаз подвесной	½"	1000	ст. Б: 866 от А	в раме инсталляции
К1-8	С_08 унитаз подвесной	Ø110	220	ст. Б: 716 от А	
В1-9	С_09 умывальник	½"	550	ст. А: 636 от Г	межос. 100
Т3-6	С_09 умывальник	½"	550	ст. А: 536 от Г	межос. 100
К1-9	С_09 умывальник	Ø50	500	ст. А: 586 от Г	
В1-10	М_15 мойка кухонная	½"	600	ст. А: 475 от Г	межос. 100
Т3-7	М_15 мойка кухонная	½"	600	ст. А: 375 от Г	межос. 100
К1-10	М_15 мойка кухонная	Ø50	400	ст. А: 425 от Г	
В1-11	М_16 посудомоечная машина	½"	550	ст. А: 725 от Г	кран ПММ в шкафу мойки
К1-11	М_16 посудомоечная машина	Ø40	550	ст. А: 625 от Г	слив ПММ в шкафу мойки


Примечания

1. Привязки выводов даны от чистовых поверхностей стен (облицовка на сторону: ванная — 24 мм (штукатурка 10 + клей 5 + плитка 9); санузел гостевой 24 мм (штукатурка 10 + клей 5 + плитка 9); кухня-гостиная — 24 мм (фартук: штукатурка 10 + клей 5 + плитка 9)); эти же грани — на развёртках и в раскладке плитки. Высоты — от чистого пола помещения.
2. До черновой разводки сверить по паспорту выбранного прибора (смеситель, инсталляция, сифон).
3. Горячая вода (Т3) — слева от холодной (В1), если смотреть на прибор. Допуск установки выводов: ±5 мм в группе, ±20 мм у отдельно стоящих.
4. Расчёт систем водоснабжения и канализации и подбор оборудования выполняет проектная организация; лист задаёт места и высоты выводов.
5. С_01 ванна (В1-1, Т3-1, К1-1) — выводы в полу: пирог пола 35 мм их не укрывает (нужно 185 мм, расчёт — профиль К1 схемы разводки); до решения заказчика (подъём пола или другой смеситель / выпуск) не выполнять.
6. С_07 душ (В1-7, Т3-5, К1-7): трап в подиуме 120 мм — верх подиума у решётки трапа +0,105, к краю поднимается уклоном 15 мм/м: ступень по открытому краю 127 мм (край показан на плане); «узел 1» — на схеме разводки; подиум — предложение, согласовать с заказчиком. Водорозетки В1-7, Т3-5 — 1100 мм от пола душа, то есть 1220 мм от чистого пола помещения: стену размечают до подиума.
7. Посудомоечная машина М_16: кран и слив — отдельными выводами в шкафу мойки (не за машиной), до машины ≤ 1500 мм.
8. Прибор М_15 мойка кухонная, М_16 посудомоечная машина взят из расстановки мебели (по шкафу с мойкой).
9. Стояки в коробах/шахтах не замоноличивать; стояк К1 в коробе — звукоизоляция стояка в коробе без жёсткого контакта с трубой; к арматуре и ревизиям — люк не меньше 300×400.


					Проект: Квартира с кабинетом — М 1:50
	Лист	№ док.	Подпись	Дата	
Дизайнер	Кырлан А.С.			04.11.26	План выводов сантехники
					Стадия: П; Лист: 42; Листов: 127

выпуск 04.11.2026 № 627e1ac6ce · стр. 42 из 127


План квартиры (М 1:400)

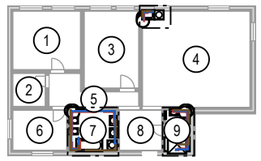


Фр. 1. Ванная (М 1:40)

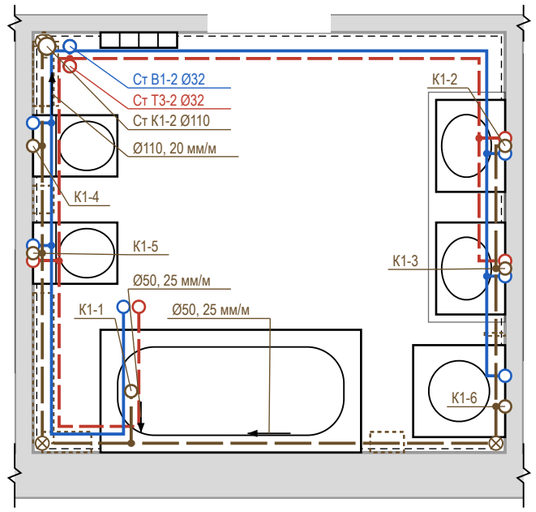


Фр. 2. Санузел гостевой (М 1:40)

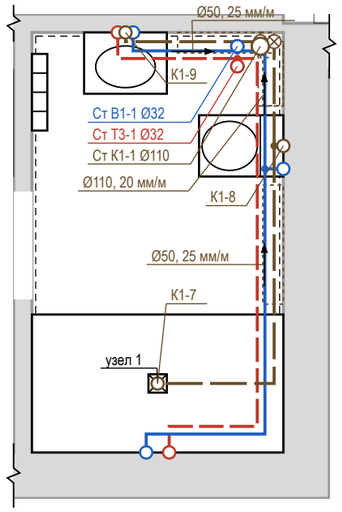

Фр. 3. Кухня-гостиная (М 1:40)

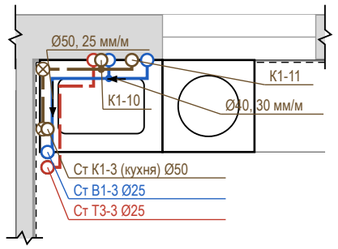

Узел 1. Душ без поддона, трап (С_07)

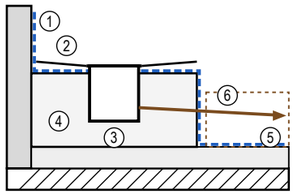

1 гидроизоляция 2 сл. на всю высоту стен душа, по всему санузлу; лента у фланца трапа и в углах
2 плитка, уклон 15 мм/м к трапу (СП 30.13330.2020, п. 17.9)
3 трап с фланцем под гидроизоляцию: монтажная высота 90 мм (до решётки) (принята, по паспорту модели)
4 подиум 120 мм у трапа, ступень 127 мм (ЦПС по гидроизоляции плиты) — предложение, согласовать с заказчиком
5 стяжка 35 мм
6 К1 Ø50, i = 25 мм/м, L = 3,11 м, Δh = 78 мм → Ст К1-1; за подиумом — короб 160×110

Пирог ≥ 168 мм = трап 90 + Δh 78 ≤ 35 + подиум 120 + плитка 14 мм

Условные обозначения


- В1 — водопровод хозяйственно-питьевой (ХВС), PP-R Ø20
- Т3 — горячее водоснабжение, подача (ГВС), PP-R Ø20
- К1 — канализация бытовая
- направление уклона К1 / пола: Ø, мм на 1 м
- ⊗ ревизия (прочистка) К1 — доступ сохранить
- ● тройник (ответвление к прибору)
- короб К1 над чистым полом (ГКЛВ под плитку)
- ○ вывод В1 (код — в ведомости привязок)
- ○ вывод Т3 (код — в ведомости привязок)
- ○ вывод К1 (код — в ведомости привязок)
- сантехприбор по расстановке (габарит модели)
- ○ стояк «Ст К1-N / Ст В1-N» (ГОСТ 21.601), Ø мм
- линия обрыва (граница фрагмента)
- граница фрагмента на плане (Фр. N)

Профиль выпусков К1 (до врезки в стояк)

Выпуск	Прибор	Ø	L, м	i, мм/м	Δh, мм	Прокладка, мм
К1-8	С_08 унитаз подвесной	Ø110	0,86	20	17	короб 160×140
К1-4	С_04 унитаз подвесной	Ø110	0,80	20	16	короб 160×140
К1-2	С_02 умывальник	Ø50	7,64	25	191	короб 280×110
К1-3	С_03 умывальник	Ø50	6,84	25	171	короб 260×110
К1-6	ОБ_03 стиральная машина	Ø50	5,94	25	149	короб 230×110
К1-1	С_01 ванна	Ø50	3,60	25	90	в полу не помещается: 185 > 35; до решения
К1-7	С_07 душ	Ø50	3,11	25	78	трап в подиуме 120 (35 + 120 + 14 ≥ 168), далее короб 160×110
К1-5	С_05 биде подвесное	Ø50	1,50	25	38	короб 120×110
К1-9	С_09 умывальник	Ø50	0,97	25	24	короб 110×110
К1-10	М_15 мойка кухонная	Ø50	0,86	25	22	над полом за приборами
К1-11	М_16 посудомоечная машина	Ø40	1,06	30	32	над полом за приборами

Короб h×b: h — от чистого пола, b — от чистовой стены. Стяжка 35 мм — лист полов.

Узел ввода В1, Т3 (по данным, без масштаба)

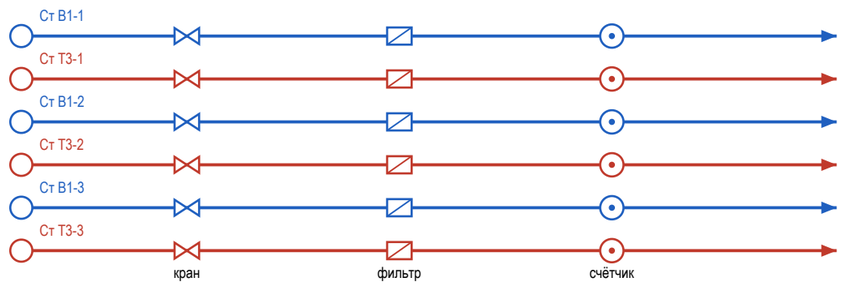

⊗ Ст К1-1, Ст К1-2, Ст К1-3 (кухня): ревизия на стояке — люк в коробе


Примечания

1. Трассы принципиальные, построены от стояков вдоль стен помещений; фактическое положение фиксируется исполнительной схемой с привязками (фото с рулеткой) до закрытия.
2. Уклон К1 не менее 1/d и не более 150 мм/м (СП 30.13330.2020, п. 19.1), приняты практические уклоны; поворот — двумя отводами 45°, ревизия после поворота, доступ сохранить. Стояк К1 в коробе — звукоизоляция стояка в коробе, без жёсткого контакта короба с трубой.
3. Решение по К1: стяжка 35 мм не укрывает трубы (нужно Ø + Δh + 45 мм) — выпуски идут над чистым полом вдоль стен: К1-10, К1-11 — за приборами и в раме инсталляции; К1-8, К1-4, К1-2, К1-3, К1-6, К1-5, К1-9 — в коробе ГКЛВ под плитку (размеры в профиле). Короба — на развёртках; отметку низа врезки в стояк замерить до черновых работ.
4. К1-7 (С_07 душ, трап): монтажная высота трапа 90 до верха решётки (по паспорту) + уклон 78 = 168 мм ≤ стяжка 35 + подиум 120 + облицовка 14 мм трап в подиуме душевой зоны (узел 1 на этом листе), за краем подиума отвод — в коробе ГКЛВ 160×110 вдоль стены; подиум — предложение, согласовать с заказчиком.
5. К1-1 (С_01 ванна, выпуск в пол): Δh 90 + Ø50 + 45 = 185 мм > пирога 35 мм — в стяжке не помещается, в короб не уходит: подиум или подъём пола на 150 мм или прибор ближе к стояку — решение заказчика; до решения не выполнять.
6. Отводы К1-2 (7,6 м), К1-3 (6,8 м), К1-6 (5,9 м) длиннее 4 м без вентиляции — у прибора воздушный клапан Ø50 в доступном месте (за люком или в тумбе) либо вентилируемый отвод (EN 12056-2, табл. 4), подбор — проектная организация.
7. Узел ввода В1, Т3 — по данным проекта: кран → фильтр → счётчик. Доступ к арматуре — через люк не меньше 300×400. Водопровод — в штробе стен или в коробах; трубы испытать давлением до закрытия (акт скрытых работ).
8. Расчёт систем, диаметры магистралей и подбор оборудования выполняет проектная организация; врезка и перенос стояков — по согласованию с управляющей организацией. Арматуру и привязки сверить по паспортам приборов.

					Проект: Квартира с кабинетом
	Лист	№ док.	Подпись	Дата	Схема разводки водопровода и канализации
Дизайнер	Кырлан А.С.			04.11.26	

Стадия	Лист	Листов
П	43	127

Схема В1 (М 1:50; по вертикали и горизонтали один масштаб, глубина — ×0,5 под 45°)

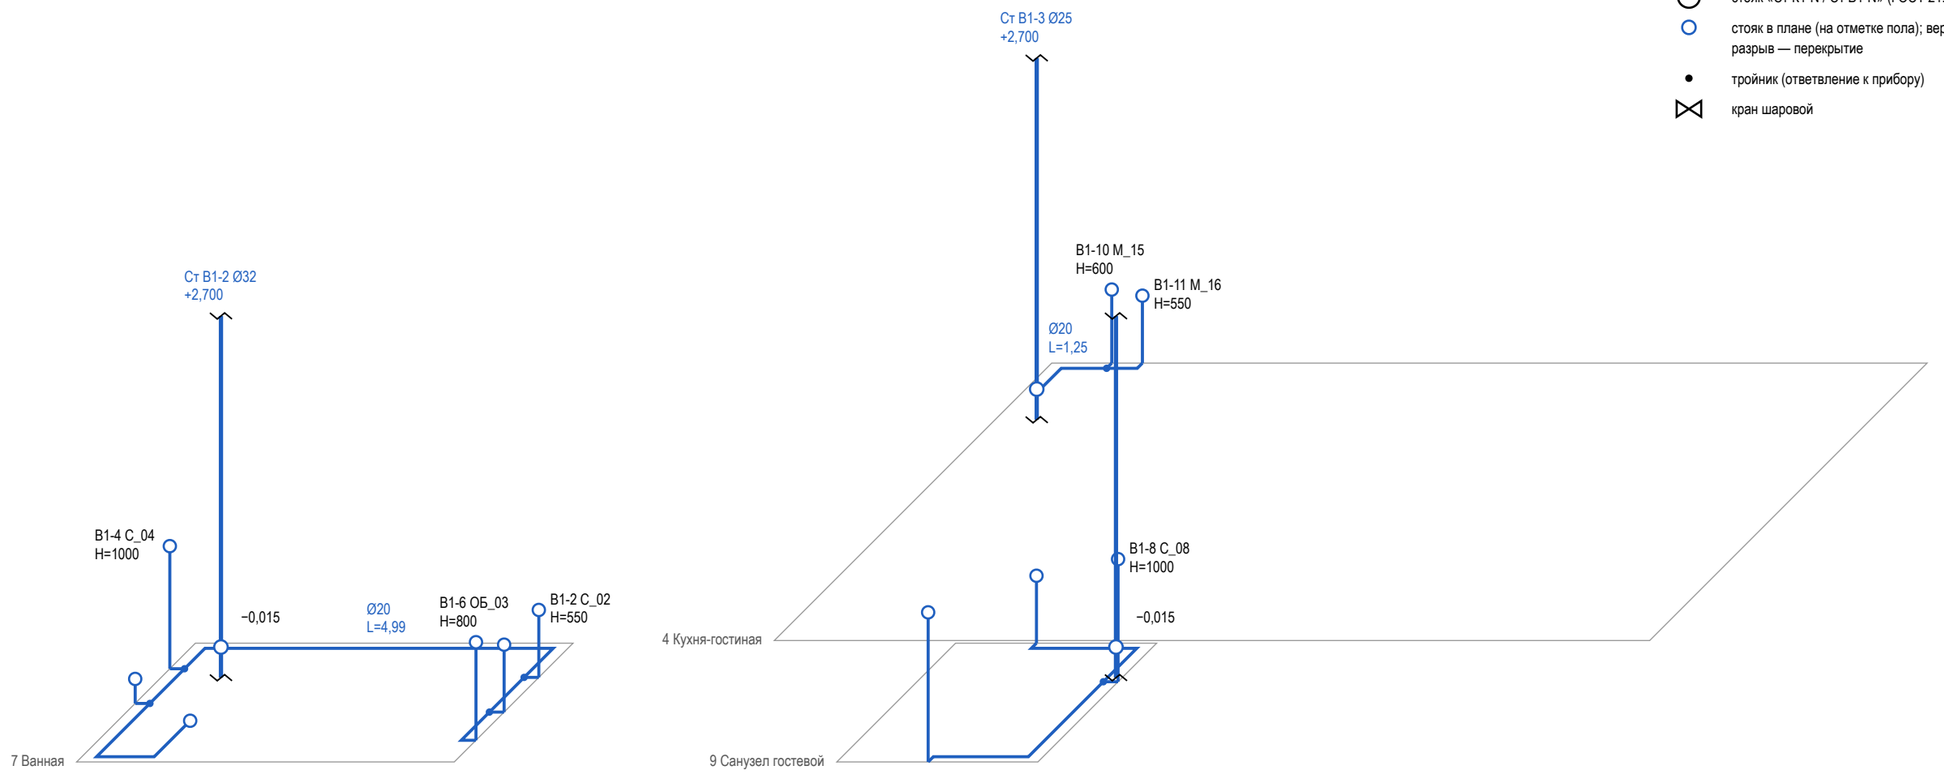

Условные обозначения

- В1 — водопровод хозяйственно-питьевой (ХВС), PP-R Ø20
- вывод В1 (код — в ведомости привязок)
- стояк «Ст К1-N / Ст В1-N» (ГОСТ 21.601), Ø мм
- стояк в плане (на отметке пола); вертикаль — стояк по высоте, разрыв — перекрытие
- тройник (ответвление к прибору)
- кран шаровой

Примечания


1. Схема В1 построена по тем же трассам, что план разводки: положение в плане сохранено, глубина — в масштабе ×0,5. Трассы принципиальные; фактическое положение фиксируется исполнительной схемой до закрытия.
2. Высоты Н — от чистого пола помещения, мм. Прокладка магистрали В1 по данным: в стяжке пола, в стяжке пола, выше плиты перекрытия; отметка трасс — по пирогу пола.
3. Узел ввода В1 (кран, фильтр, счётчик, обратный клапан, кран) — на схеме разводки; состав узла ввода — по согласованию. Кран шаровой — на первом участке от стояка.
4. Трубы испытать давлением до закрытия (акт скрытых работ, опрессовка по СП 73.13330.2016).
5. Диаметры, высоты выводов и места кранов — по паспортам выбранных приборов и расчёту проектной организации.
6. Расчёт систем, диаметры магистралей и подбор оборудования выполняет проектная организация.

					Проект: Квартира с кабинетом		М 1:50
	Лист	№ док.	Подпись	Дата	Аксонометрическая схема В1 (холодное водоснабжение)	Стадия	Лист	Листов
Дизайнер	Кырлан А.С.			04.11.26		П	44	127

Схема Т3 (М 1:50; по вертикали и горизонтали один масштаб, глубина — ×0,5 под 45°)

Условные обозначения

- Т3 — горячее водоснабжение, подача (ГВС), PP-R Ø20
- вывод Т3 (код — в ведомости привязок)
- стояк «Ст К1-N / Ст В1-N» (ГОСТ 21.601), Ø мм
- стояк в плане (на отметке пола); вертикаль — стояк по высоте, разрыв — перекрытие
- тройник (ответвление к прибору)
- кран шаровой

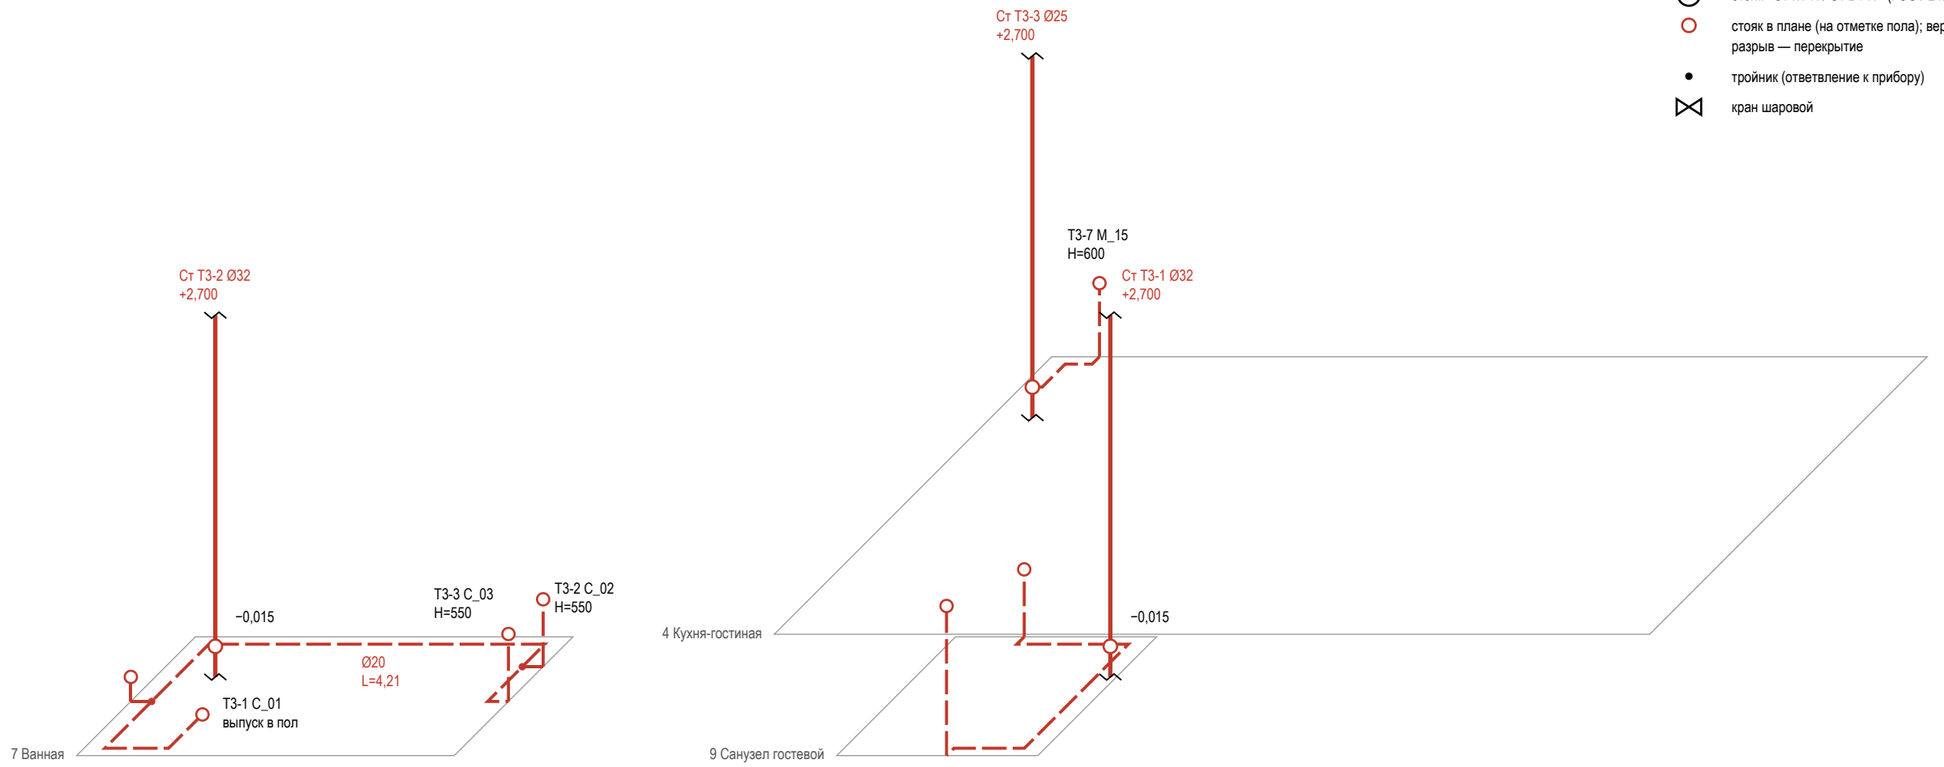


Примечания

1. Схема Т3 построена по тем же трассам, что план разводки: положение в плане сохранено, глубина — в масштабе ×0,5. Трассы принципиальные; фактическое положение фиксируется исполнительной схемой до закрытия.
2. Высоты Н — от чистого пола помещения, мм. Прокладка магистрали Т3 по данным: в стяжке пола, в стяжке пола, выше плиты перекрытия; отметка трасс — по пирогу пола.
3. Узел ввода Т3 (кран, фильтр, счётчик, обратный клапан, кран) — на схеме разводки; состав узла ввода — по согласованию. Кран шаровой — на первом участке от стояка.
4. Циркуляция ГВС в данных не задана — циркуляционного трубопровода на схеме нет.
5. Трубы испытать давлением до закрытия (акт скрытых работ, опрессовка по СП 73.13330.2016).
6. Диаметры, высоты выводов и места кранов — по паспортам выбранных приборов и расчёту проектной организации.
7. Расчёт систем, диаметры магистралей и подбор оборудования выполняет проектная организация.

					Проект: Квартира с кабинетом	**М 1:50**
	Лист	№ док.	Подпись	Дата	Аксонометрическая схема Т3 (горячее водоснабжение)	Стадия / Лист / Листов
Дизайнер	Кырлан А.С.			04.11.26		П / 45 / 127

Схема К1 (М 1:50; по вертикали и горизонтали один масштаб, глубина — ×0,5 под 45°)

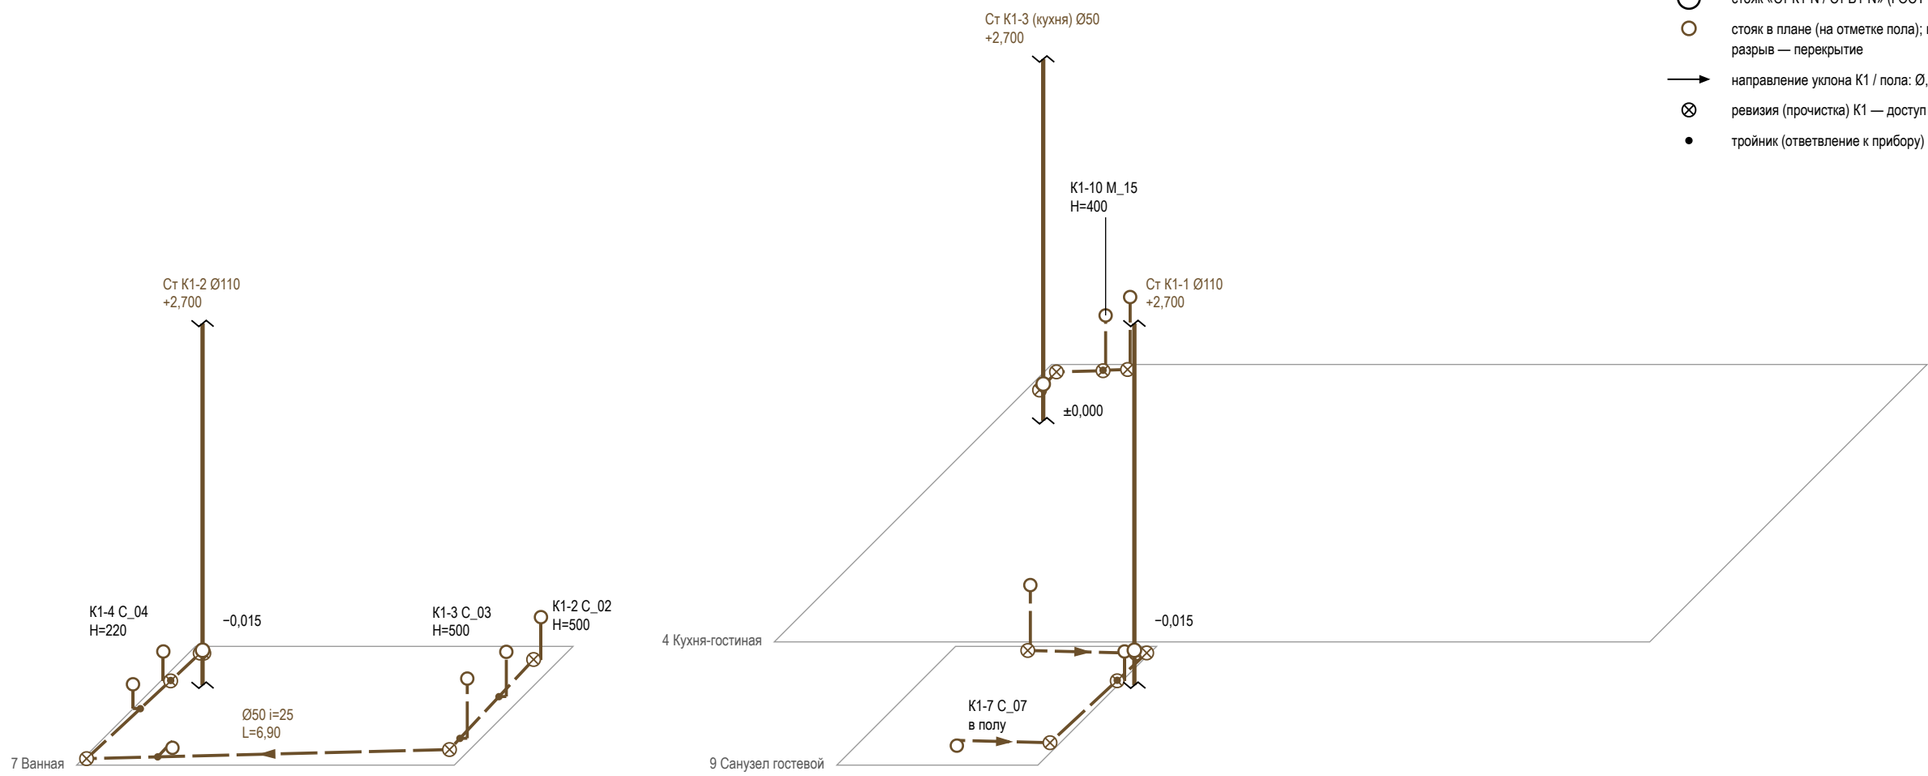

Условные обозначения


- К1 — канализация бытовая
- вывод К1 (код — в ведомости привязок)
- стояк «Ст К1-N / Ст В1-N» (ГОСТ 21.601), Ø мм
- стояк в плане (на отметке пола); вертикаль — стояк по высоте, разрыв — перекрытие
- направление уклона К1 / пола: Ø, мм на 1 м
- ревизия (прочистка) К1 — доступ сохранить
- тройник (ответвление к прибору)

Примечания

1. Схема К1 построена по тем же трассам, что план разводки: положение в плане сохранено, глубина — в масштабе ×0,5. Трассы принципиальные; фактическое положение фиксируется исполнительной схемой до закрытия.
2. Отметки — от плиты перекрытия: низ трубы у врезки в стояк — отметка из данных выпуска, к прибору труба поднимается на уклон i, мм/м (уклон не менее 1/d и не более 150 мм/м, СП 30.13330.2020, п. 19.1); чистый пол — выше плиты на стяжку (высота пирога пола). Высота выпуска прибора Н — от чистого пола.
3. Ревизия — на повороте и в начале участка; стояк К1 в коробе с люком — звукоизоляция стояка в коробе; поворот — двумя отводами 45°.
4. Трубы испытать давлением до закрытия (акт скрытых работ, опрессовка по СП 73.13330.2016).
5. Диаметры, высоты выводов и места кранов — по паспортам выбранных приборов и расчёту проектной организации.
6. Расчёт систем, диаметры магистралей и подбор оборудования выполняет проектная организация.

					Проект: Квартира с кабинетом	М 1:50
	Лист	№ док.	Подпись	Дата		
Дизайнер	Кырлан А.С.			04.11.26	Аксонометрическая схема К1 (канализация)	Стадия: П; Лист: 46; Листов: 127

Стена А (М 1:25)

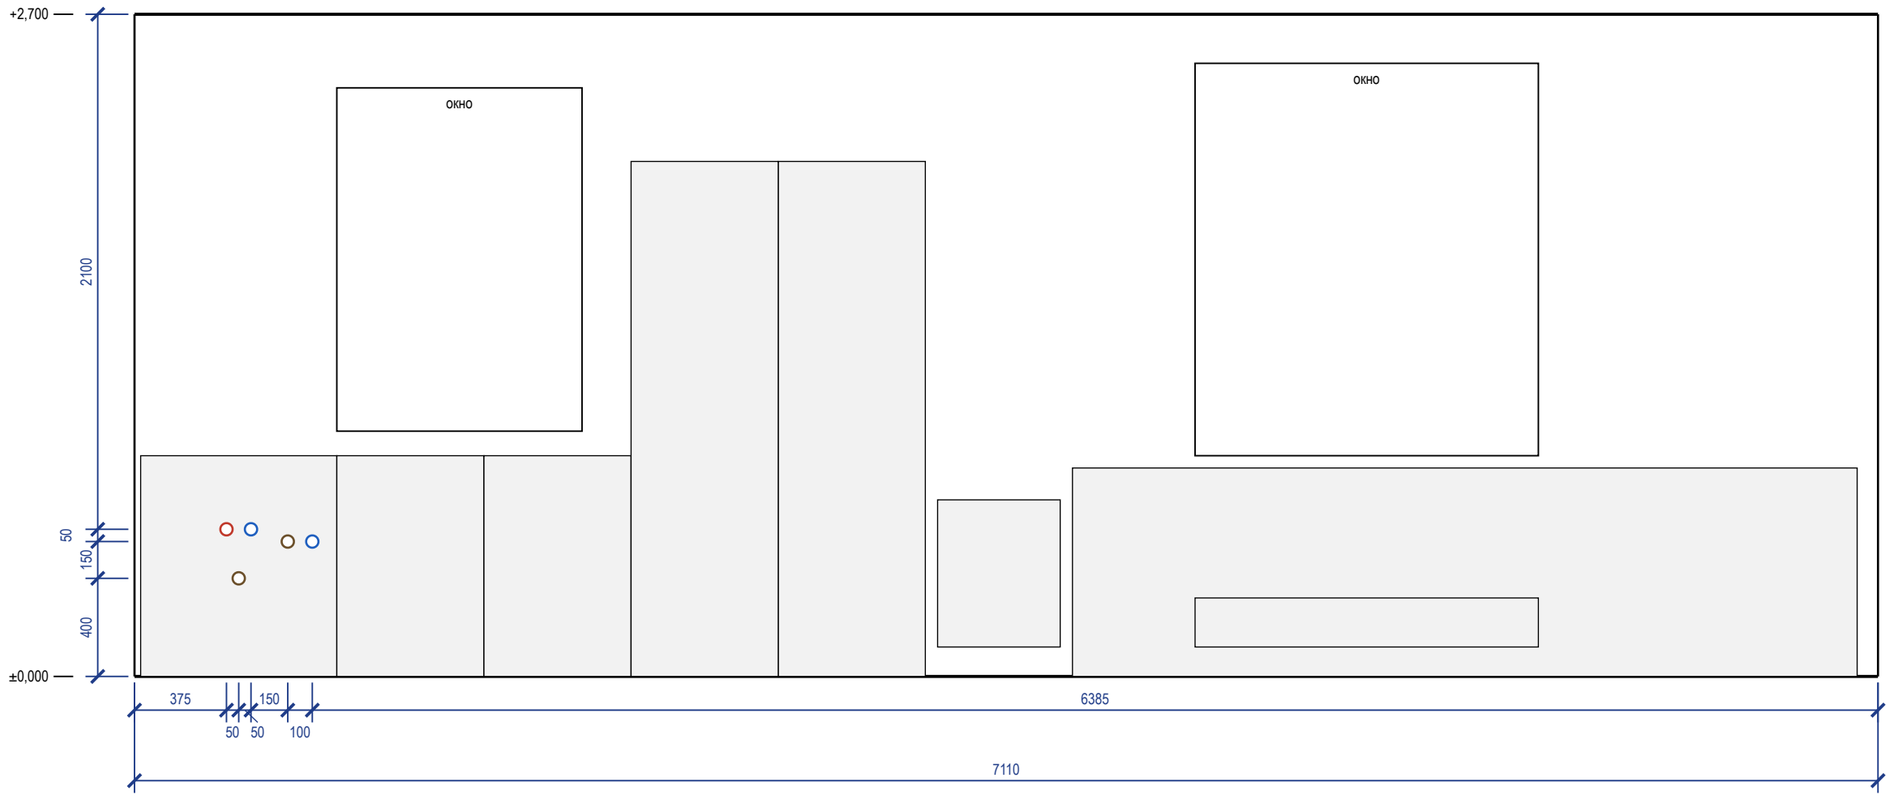

Ведомость привязок выводов (от чистого пола и угла)

Код	Прибор	Ø	H, мм	Привязка, мм
В1-10	М_15 мойка кухонная	½"	600	ст. А: 475 от лев. угла
Т3-7	М_15 мойка кухонная	½"	600	ст. А: 375 от лев. угла
К1-10	М_15 мойка кухонная	Ø50	400	ст. А: 425 от лев. угла
В1-11	М_16 посудомоечная машина	½"	550	ст. А: 725 от лев. угла
К1-11	М_16 посудомоечная машина	Ø40	550	ст. А: 625 от лев. угла

Условные обозначения


- вывод В1 (код — в ведомости привязок)
- вывод Т3 (код — в ведомости привязок)
- вывод К1 (код — в ведомости привязок)
- сантехприбор по расстановке (габарит модели)
- дверной проём; окно — сплошной контур

Примечания


1. Габариты и высоты приборов, межосевые смесителей и места кранов — по паспортам выбранных приборов, сверяются до разметки стен.
2. Высоты H — от чистого пола помещения, мм; отметка чистого пола и потолка — у левого края вида (от ±0,000 объекта). Привязки — от левого чистового угла вида (облицовка стен вычтена), как на развёртках стен.
3. Стояки в помещении: Ст К1-3 (кухня) Ø50, Ст В1-3 Ø25, Ст Т3-3 Ø25 — положение на плане выводов; выводы подключаются к ним по схеме разводки.
4. Ревизионные люки (арматура и ревизии у М_15, М_16 300×400, стена А у М_15, предложение): привязка к углу — по раскладке плитки, подтверждается обмером.
5. Ревизионные люки к арматуре и ревизиям в данных не заданы: место и размер не определены (записи реестра нет).
6. Мойка, ПММ и фильтр — выводы в шкафу мойки; диаметры и положение сифона и кранов сверить по паспортам приборов и чертежам модуля.
7. Часть подписей выводов не уместилась у знака: коды и высоты — в ведомости привязок.
8. Расчёт систем водоснабжения и канализации и подбор оборудования выполняет проектная организация; лист задаёт места и высоты выводов.

					Проект: Квартира с кабинетом	М 1:25
	Лист	№ док.	Подпись	Дата		
Дизайнер	Кырлан А.С.			04.11.26	Развёртки мокрых зон: выводы ВК. Кухня-гостиная	Стадия: П; Лист: 47; Листов: 127

Стена А (М 1:20)

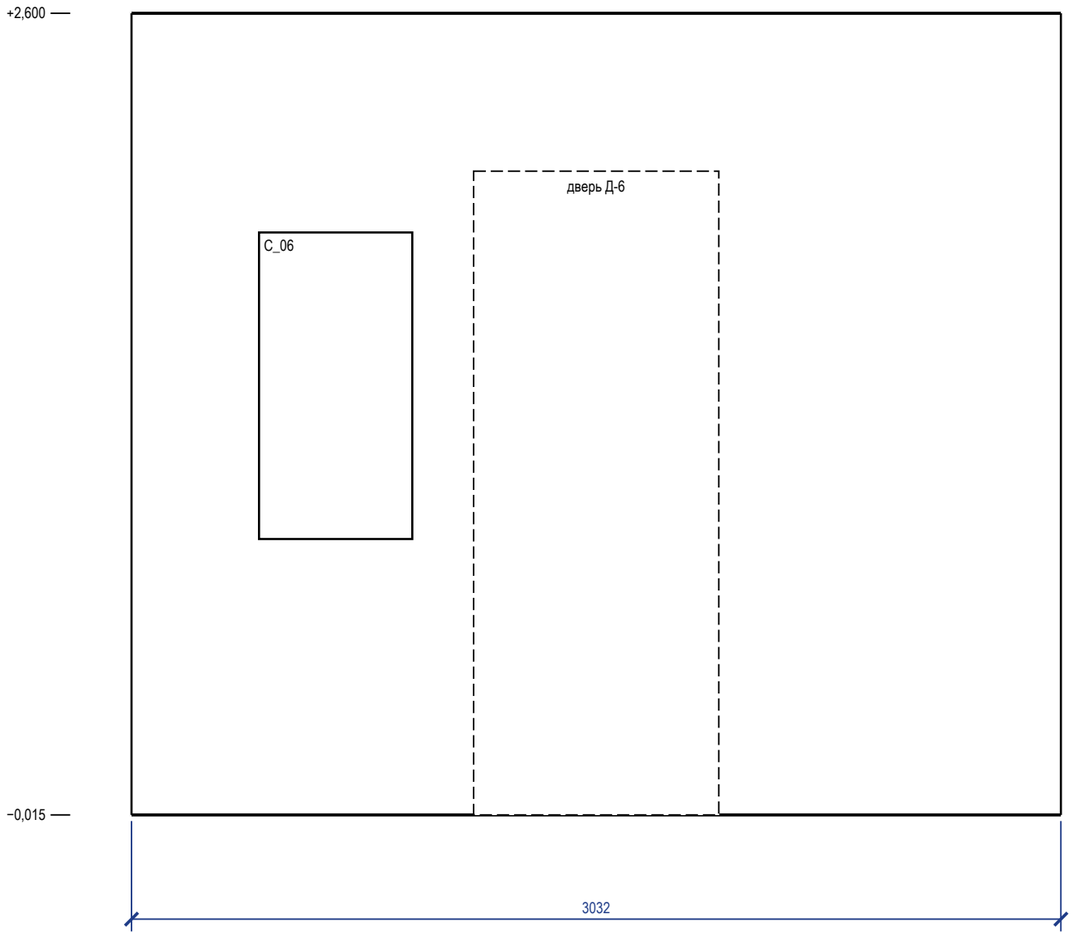

Стена Б (М 1:20)

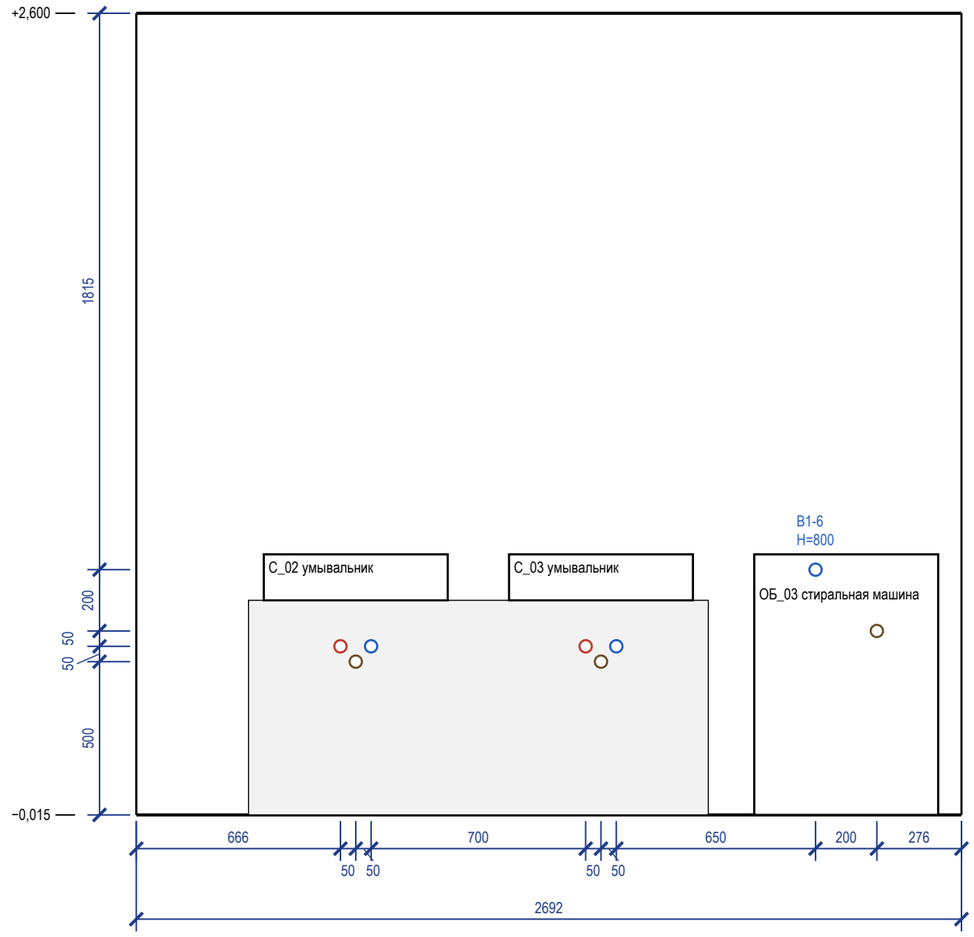

Ведомость привязок выводов (от чистого пола и угла)

Код	Прибор	Ø	H, мм	Привязка, мм
В1-2	С_02 умывальник	½"	550	ст. Б: 766 от лев. угла
Т3-2	С_02 умывальник	½"	550	ст. Б: 666 от лев. угла
К1-2	С_02 умывальник	Ø50	500	ст. Б: 716 от лев. угла
В1-3	С_03 умывальник	½"	550	ст. Б: 1566 от лев. угла

Ведомость привязок (продолжение)

Код	Прибор	Ø	H, мм	Привязка, мм
Т3-3	С_03 умывальник	½"	550	ст. Б: 1466 от лев. угла
К1-3	С_03 умывальник	Ø50	500	ст. Б: 1516 от лев. угла
В1-6	ОБ_03 стиральная машина	½"	800	ст. Б: 2216 от лев. угла
К1-6	ОБ_03 стиральная машина	Ø50	600	ст. Б: 2416 от лев. угла

Условные обозначения

- вывод В1 (код — в ведомости привязок)
- вывод Т3 (код — в ведомости привязок)
- вывод К1 (код — в ведомости привязок)
- сантехприбор по расстановке (габарит модели)
- дверной проём; окно — сплошной контур


Примечания

1. Габариты и высоты приборов, межосевые смесителей и места кранов — по паспортам выбранных приборов, сверяются до разметки стен.
2. Высоты H — от чистого пола помещения, мм; отметка чистого пола и потолка — у левого края вида (от ±0,000 объекта). Привязки — от левого чистового угла вида (облицовка стен вычтена), как на развёртках стен.
3. Выводы в полу (В1-1, Т3-1, К1-1): трап, лоток, выпуск отдельностоящей ванны, подвод к стойке напольного смесителя — на развёртке их нет; место и пирог пола — лист «Схема разводки» (профиль К1, узел 1).
4. Стояки в помещении: Ст К1-2 Ø110, Ст В1-2 Ø32, Ст Т3-2 Ø32 — положение на плане выводов; выводы подключаются к ним по схеме разводки.
5. Ревизионные люки (арматура и ревизии у С_01 300×400, стена В у С_01, предложение): привязка к углу — по раскладке плитки, подтверждается обмером.
6. Ревизионные люки к арматуре и ревизиям в данных не заданы: место и размер не определены (записи реестра нет).
7. Часть подписей выводов не уместилась у знака: коды и высоты — в ведомости привязок.
8. Помещение «Ванная» — 2 листа: стены 1) А, Б; 2) В, Г.
9. Расчёт систем водоснабжения и канализации и подбор оборудования выполняет проектная организация; лист задаёт места и высоты выводов.


					Проект: Квартира с кабинетом	М 1:20
	Лист	№ док.	Подпись	Дата	Развёртки мокрых зон: выводы ВК. Ванная (лист 1 из 2)	
Дизайнер	Кырлан А.С.			04.11.26		

Стадия	Лист	Листов
П	48	127

Стена В (М 1:20)

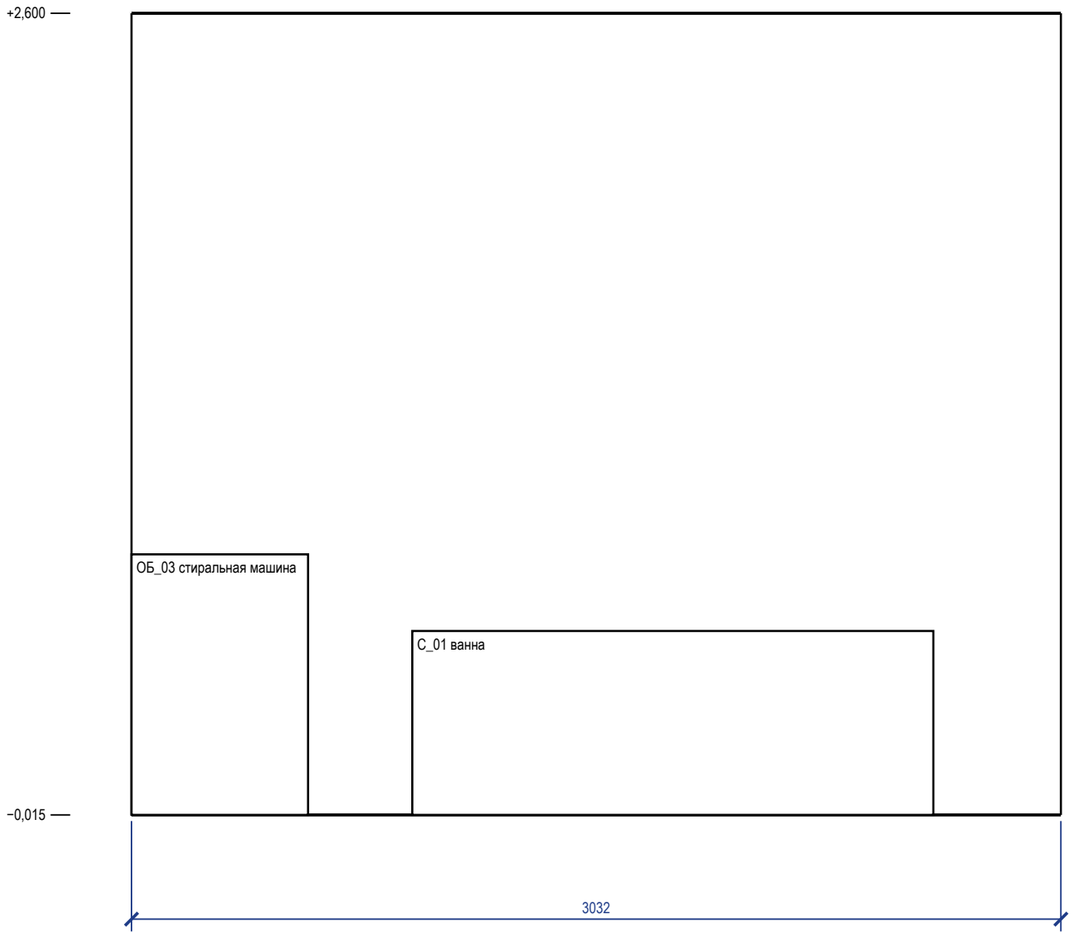

Стена Г (М 1:20)

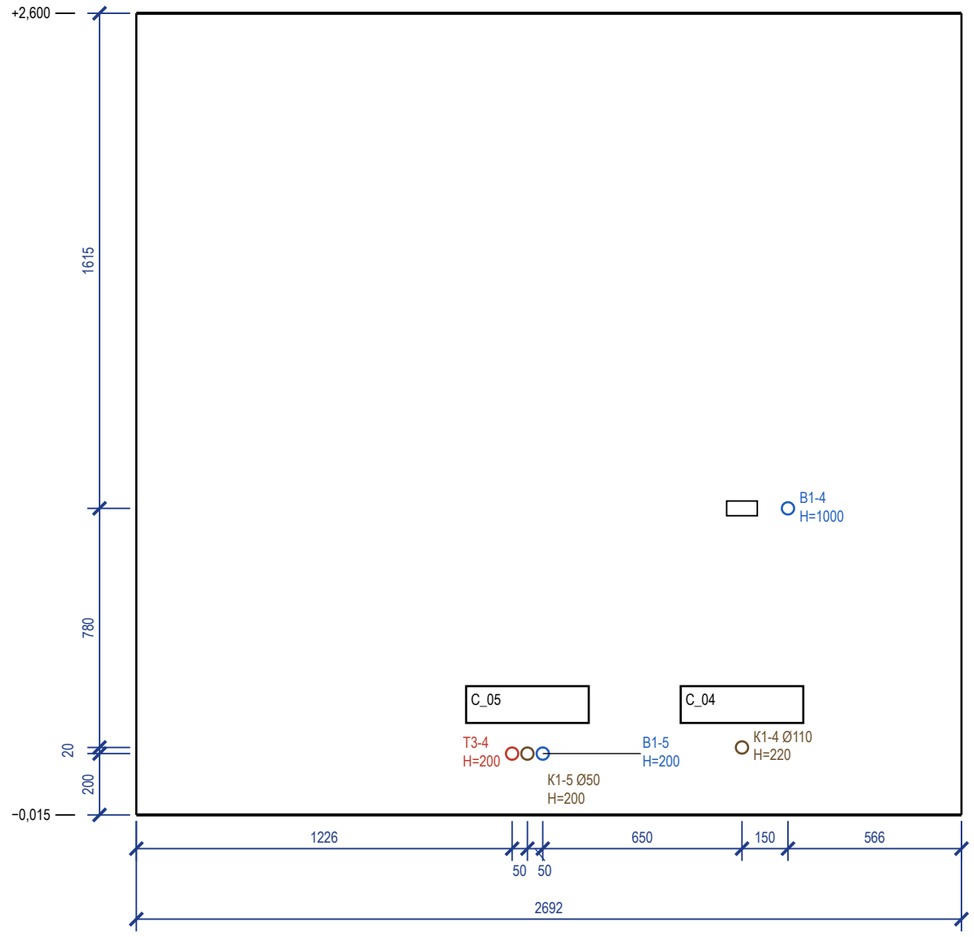

Ведомость привязок выводов (от чистого пола и угла)

Код	Прибор	Ø	Н, мм	Привязка, мм
В1-4	С_04 унитаз подвесной	½"	1000	ст. Г: 2126 от лев. угла
К1-4	С_04 унитаз подвесной	Ø110	220	ст. Г: 1976 от лев. угла
В1-5	С_05 биде подвесное	½"	200	ст. Г: 1326 от лев. угла

Ведомость привязок (продолжение)

Код	Прибор	Ø	Н, мм	Привязка, мм
Т3-4	С_05 биде подвесное	½"	200	ст. Г: 1226 от лев. угла
К1-5	С_05 биде подвесное	Ø50	200	ст. Г: 1276 от лев. угла

Условные обозначения

- вывод В1 (код — в ведомости привязок)
- вывод Т3 (код — в ведомости привязок)
- вывод К1 (код — в ведомости привязок)
- сантехприбор по расстановке (габарит модели)
- дверной проём; окно — сплошной контур
- кнопка смыва инсталляции (Н — по данным прибора)

Примечания

1. Габариты и высоты приборов, межосевые смесителей и места кранов — по паспортам выбранных приборов, сверяются до разметки стен.
2. Высоты Н — от чистого пола помещения, мм; отметка чистого пола и потолка — у левого края вида (от ±0,000 объекта). Привязки — от левого чистового угла вида (облицовка стен вычтена), как на развёртках стен.
3. Кнопка смыва С_04 — Н=1000 (по данным прибора).
4. Выводы в полу (В1-1, Т3-1, К1-1): трап, лоток, выпуск отдельностоящей ванны, подвод к стойке напольного смесителя — на развёртке их нет; место и пирог пола — лист «Схема разводки» (профиль К1, узел 1).
5. Стояки в помещении: Ст К1-2 Ø110, Ст В1-2 Ø32, Ст Т3-2 Ø32 — положение на плане выводов; выводы подключаются к ним по схеме разводки.
6. Ревизионные люки (арматура и ревизии у С_01 300×400, стена В у С_01, предложение): привязка к углу — по раскладке плитки, подтверждается обмером.
7. Ревизионные люки к арматуре и ревизиям в данных не заданы: место и размер не определены (записи реестра нет).
8. Помещение «Ванная» — 2 листа: стены 1) А, Б; 2) В, Г.
9. Расчёт систем водоснабжения и канализации и подбор оборудования выполняет проектная организация; лист задаёт места и высоты выводов.

	Лист	№ док.	Подпись	Дата
Дизайнер	Кырлан А.С.			04.11.26


Проект: Квартира с кабинетом — **М 1:20**

Развёртки мокрых зон: выводы ВК. Ванная (лист 2 из 2)


Стадия	Лист	Листов
П	49	127

выпуск 04.11.2026 № 627e1ac6ce · стр. 49 из 127

Стена А (М 1:20)

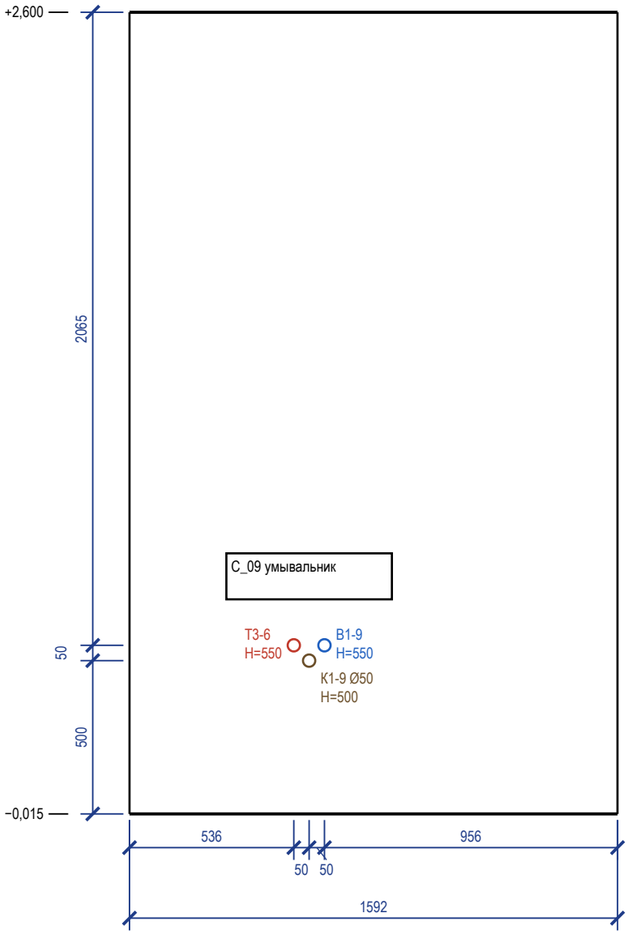

Стена Б (М 1:20)

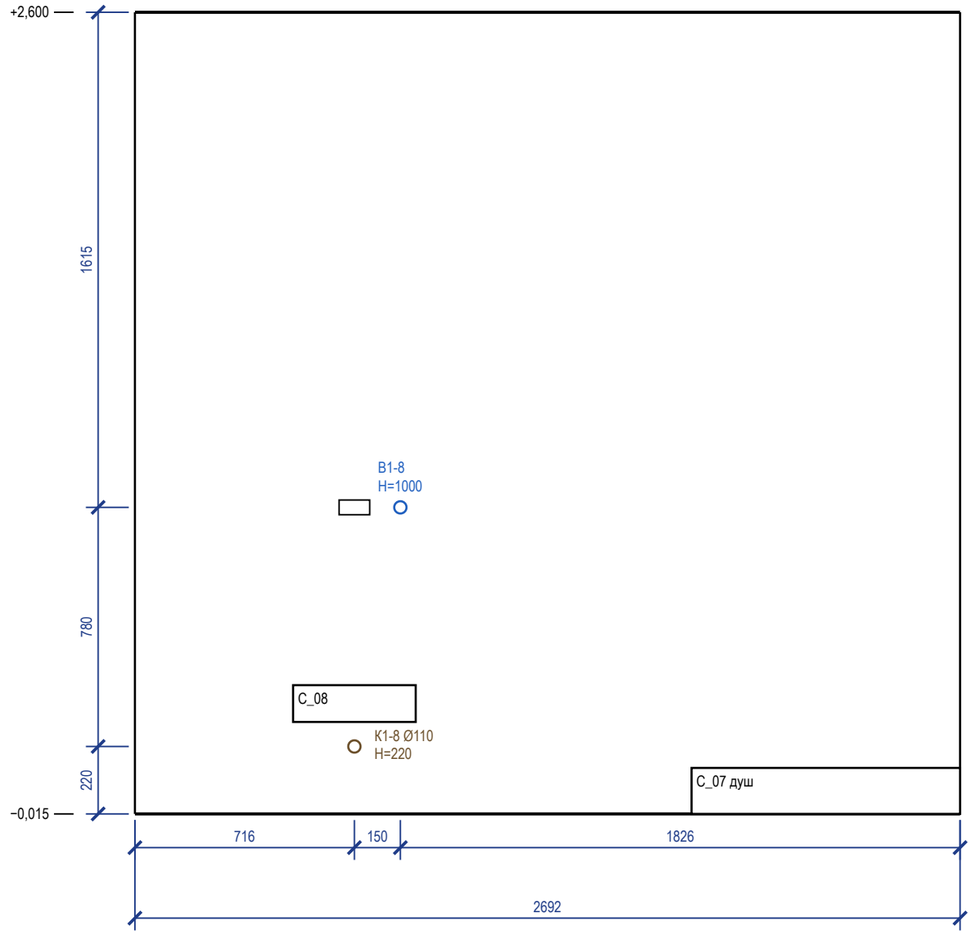

Ведомость привязок выводов (от чистого пола и угла)

Код	Прибор	Ø	H, мм	Привязка, мм
B1-9	C_09 умывальник	½"	550	ст. А: 636 от лев. угла
T3-6	C_09 умывальник	½"	550	ст. А: 536 от лев. угла
K1-9	C_09 умывальник	Ø50	500	ст. А: 586 от лев. угла

Ведомость привязок (продолжение)

Код	Прибор	Ø	H, мм	Привязка, мм
B1-8	C_08 унитаз подвесной	½"	1000	ст. Б: 866 от лев. угла
K1-8	C_08 унитаз подвесной	Ø110	220	ст. Б: 716 от лев. угла

Условные обозначения


- вывод B1 (код — в ведомости привязок)
- вывод T3 (код — в ведомости привязок)
- вывод K1 (код — в ведомости привязок)
- сантехприбор по расстановке (габарит модели)
- дверной проём; окно — сплошной контур
- кнопка смыва инсталляции (H — по данным прибора)

Примечания


1. Габариты и высоты приборов, межосевые смесителей и места кранов — по паспортам выбранных приборов, сверяются до разметки стен.
2. Высоты H — от чистого пола помещения, мм; отметка чистого пола и потолка — у левого края вида (от ±0,000 объекта). Привязки — от левого чистового угла вида (облицовка стен вычтена), как на развёртках стен.
3. Кнопка смыва C_08 — H=1000 (по данным прибора).
4. Выводы в полу (K1-1): трап, лоток, выпуск отдельностоящей ванны, подвод к стойке напольного смесителя — на развёртке их нет; место и пирог пола лист «Схема разводки» (профиль K1, узел 1).
5. Стояки в помещении: Ст K1-1 Ø110, Ст B1-1 Ø32, Ст T3-1 Ø32 — положение на плане выводов; выводы подключаются к ним по схеме разводки.
6. Ревизионные люки (арматура и ревизии у C_07 300×400, стена В у C_07, предложение): привязка к углу — по раскладке плитки, подтверждается обмером.
7. Ревизионные люки к арматуре и ревизиям в данных не заданы: место и размер не определены (записи реестра нет).
8. Помещение «Санузел гостевой» — 2 листа: стены 1) А, Б; 2) В, Г.
9. Расчёт систем водоснабжения и канализации и подбор оборудования выполняет проектная организация; лист задаёт места и высоты выводов.

					Проект: Квартира с кабинетом — М 1:20
	Лист	№ док.	Подпись	Дата	Развёртки мокрых зон: выводы ВК. Санузел гостевой (лист 1 из 2)
Дизайнер	Кырлан А.С.			04.11.26	Стадия: П · Лист: 50 · Листов: 127

Стена В (М 1:20)

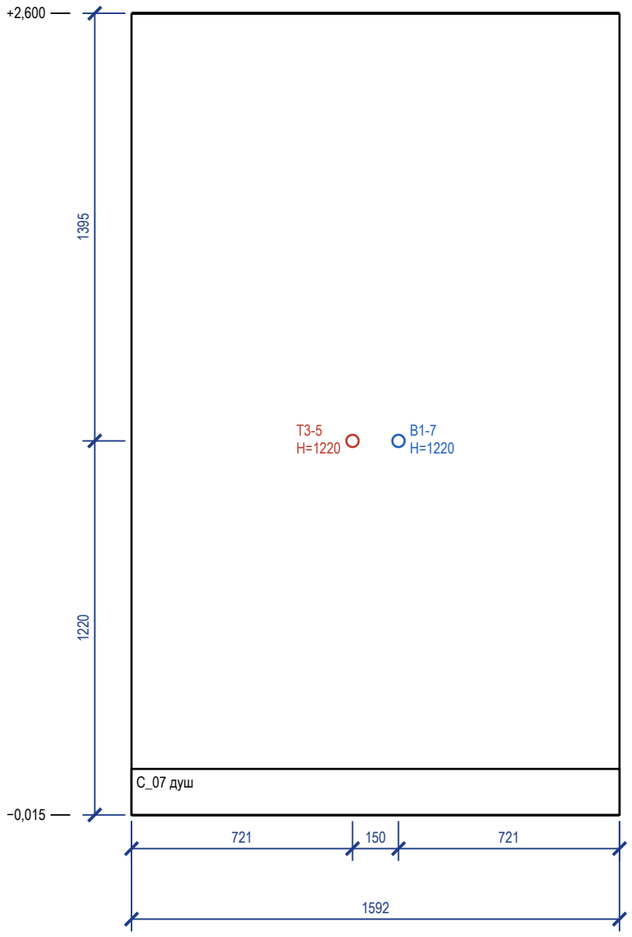

Стена Г (М 1:20)

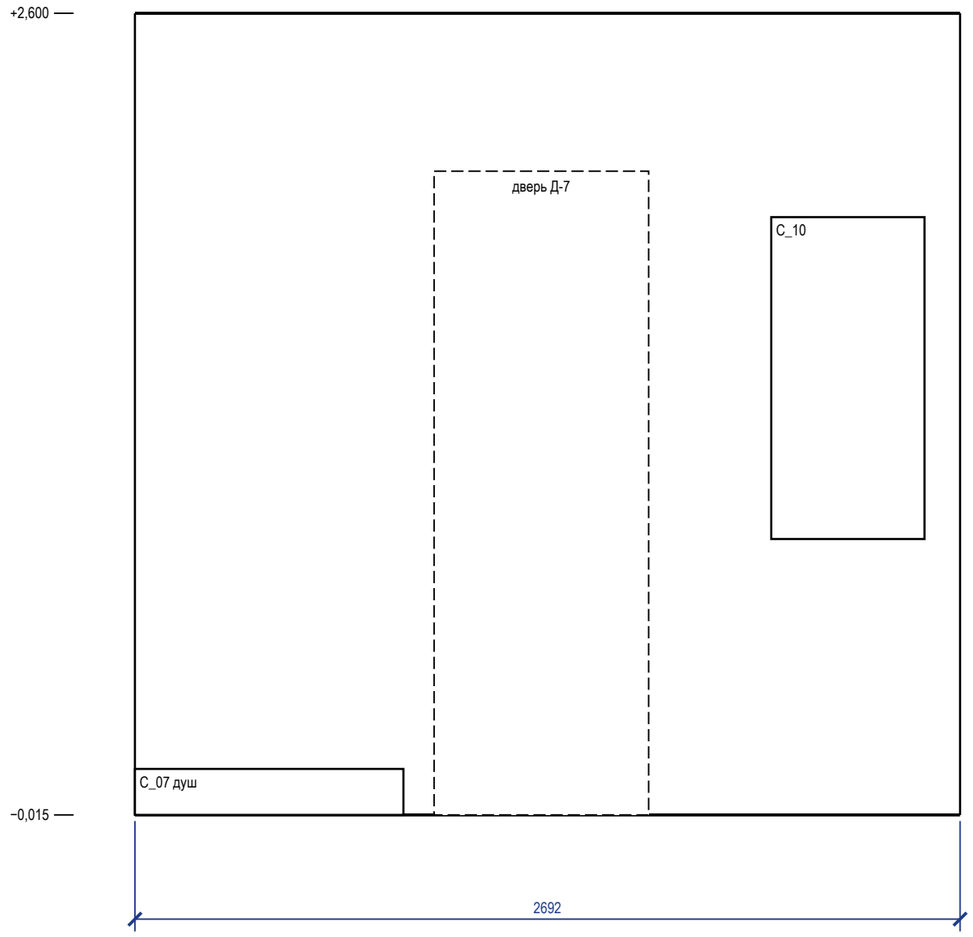

Ведомость привязок выводов (от чистого пола и угла)

Код	Прибор	Ø	H, мм	Привязка, мм
B1-7	C_07 душ	½"	1220	ст. В: 871 от лев. угла
T3-5	C_07 душ	½"	1220	ст. В: 721 от лев. угла

Условные обозначения

- вывод B1 (код — в ведомости привязок)
- вывод T3 (код — в ведомости привязок)
- вывод K1 (код — в ведомости привязок)
- сантехприбор по расстановке (габарит модели)
- дверной проём; окно — сплошной контур

Примечания

1. Габариты и высоты приборов, межосевые смесителей и места кранов — по паспортам выбранных приборов, сверяются до разметки стен.
2. Высоты Н — от чистого пола помещения, мм; отметка чистого пола и потолка — у левого края вида (от ±0,000 объекта). Привязки — от левого чистового угла вида (облицовка стен вычтена), как на развёртках стен.
3. Выводы в полу (К1-1): трап, лоток, выпуск отдельностоящей ванны, подвод к стойке напольного смесителя — на развёртке их нет; место и пирог пола лист «Схема разводки» (профиль К1, узел 1).
4. Стояки в помещении: Ст К1-1 Ø110, Ст В1-1 Ø32, Ст Т3-1 Ø32 — положение на плане выводов; выводы подключаются к ним по схеме разводки.
5. Ревизионные люки (арматура и ревизии у С_07 300×400, стена В у С_07, предложение): привязка к углу — по раскладке плитки, подтверждается обмером.
6. Ревизионные люки к арматуре и ревизиям в данных не заданы: место и размер не определены (записи реестра нет).
7. Помещение «Санузел гостевой» — 2 листа: стены 1) А, Б; 2) В, Г.
8. Расчёт систем водоснабжения и канализации и подбор оборудования выполняет проектная организация; лист задаёт места и высоты выводов.

	Лист	№ док.	Подпись	Дата
Дизайнер	Кырлан А.С.			04.11.26

Проект: Квартира с кабинетом — **М 1:20**

Развёртки мокрых зон: выводы ВК. Санузел гостевой (лист 2 из 2)

Стадия	Лист	Листов
П	51	127


Поз.	Наименование и техническая характеристика	Тип, марка, обозначение документа	Код продукции	Поставщик	Ед. изм.	Кол.	Масса 1 ед., кг	Примечание
	Санитарные приборы							
1	Ванна отдельностоящая из литого камня 1700×800 мм, выпуск в пол; донный клапан, перелив и сифон отдельной позицией	ванна отдельностоящая овальная 1700×800, литой камень; смеситель напольный		выбор заказчика	шт	1		C_01
2	Унитаз подвесной безободковый, с сиденьем микролифт, крепёж и звукоизолирующая прокладка	Jacob Delafon Struktura EDF102-00		выбор заказчика	шт	2		C_04, C_08
3	Инсталляция для подвесного унитаза: рама высотой 1120 мм, бачок, клавиша смыва (ось клавиши 1050 мм от чистого пола)	аналог		выбор заказчика	шт	2		C_04 — короб ГКЛВ общий с C_05; C_08 короб ГКЛВ
4	Раковина накладная 600×450 мм, на столешницу тумбы, с переливом	раковина накладная овальная, две на тумбе 1500		выбор заказчика	шт	2		C_02, C_03
5	Умывальник из травертина 540×400 мм на консоли, с переливом	раковина 540 на консоли, травертин		выбор заказчика	шт	1		C_09
6	Биде подвесное, крепёж и звукоизолирующая прокладка	биде подвесное		выбор заказчика	шт	1		C_05
7	Инсталляция для подвесного биде: рама с крепёжными шпильками, водорозетками ½" (ХВ, ГВ) и выпуском Ø50	аналог		выбор заказчика	шт	1		C_05; короб ГКЛВ общий с C_04
8	Трап душевой с гидрозатвором и фланцем под гидроизоляцию, монтажная высота по паспорту	аналог		выбор заказчика	шт	1		C_07; узел 1 схема разводки
9	Мойка кухонная врезная / подстольная, с переливом, ориентир 700×480 мм — в модуле M_15 шириной 800 мм, вырез по шаблону модели	аналог		с кухонной мебелью	шт	1		M_15
10	Полотенцесушитель электрический, IP44, с терморегулятором	аналог		выбор заказчика	шт	2		C_06, C_10
	Смесители, сифоны и арматура приборов							
11	Смеситель для ванны напольный (стойка) однорычажный, с ручным душем; встраиваемая часть в пол — до стяжки	аналог		выбор заказчика	шт	1		C_01
12	Смеситель для накладной раковины однорычажный, высокий излив, с донным клапаном	аналог		выбор заказчика	шт	2		C_02, C_03
13	Смеситель для умывальника однорычажный, с донным клапаном	аналог		выбор заказчика	шт	1		C_09
14	Душевая система скрытого монтажа с термостатом: встраиваемая часть, верхний душ, ручная лейка	аналог		выбор заказчика	шт	1		C_07; встраиваемая часть — до плитки
15	Смеситель кухонный однорычажный, высокий излив	аналог		выбор заказчика	шт	1		M_15
16	Смеситель для биде однорычажный, с донным клапаном	аналог		выбор заказчика	шт	1		C_05
17	Сифон для отдельностоящей ванны с донным клапаном и переливом, выпуск в пол Ø40/50	аналог		выбор заказчика	шт	1		C_01
18	Сифон для умывальника бутылочный Ø32/40–50, с гофрой к выпуску	аналог		выбор заказчика	шт	3		C_02, C_03, C_09
19	Сифон для биде Ø32/40–50	аналог		выбор заказчика	шт	1		C_05
20	Сифон для мойки Ø40/50	аналог		выбор заказчика	шт	1		M_15
21	Сифон для посудомоечной машины с обратным клапаном, на выводе слива Ø40	аналог		выбор заказчика	шт	1		M_16
22	Сифон для стиральной машины встраиваемый в стену Ø50, с обратным клапаном	аналог		выбор заказчика	шт	1		ОБ_03
23	Кран угловой ½"×½" с гибкой подводкой 40 см (умывальники, биде, мойка)	аналог		выбор заказчика	шт	10		по 2 на прибор
24	Кран шаровой угловой ½"×¾" для подключения стиральной и посудомоечной машины	аналог		выбор заказчика	шт	2		ОБ_03, M_16
	Трубопроводы							
25	Труба полипропиленовая PP-R PN20 Ø20×3,4 (B1)	ГОСТ 32415-2013		выбор заказчика	м	25	0,17	15,3 + 7,0 + 10 %
26	Труба PP-R, армированная стекловолокном, PN20 Ø20×2,8 (Т3)	ГОСТ 32415-2013		выбор заказчика	м	19	0,15	13,6 + 3,7 + 10 %
27	Труба канализационная ПП Ø40 (К1)	ГОСТ 32414-2013		выбор заказчика	м	1		0,3 + 0,6 + 10 %
28	Труба канализационная ПП Ø50 (К1)	ГОСТ 32414-2013		выбор заказчика	м	16		11,5 + 2,8 + 10 %
29	Труба канализационная ПП Ø110 (К1)	ГОСТ 32414-2013		выбор заказчика	м	2,5		1,7 + 0,4 + 10 %
	Фасонные части и выводы							
30	Отвод канализационный ПП 45° Ø40	ГОСТ 32414-2013		выбор заказчика	шт	2		2 шт. на поворот
31	Отвод канализационный ПП 45° Ø50	ГОСТ 32414-2013		выбор заказчика	шт	16		2 шт. на поворот
32	Отвод канализационный ПП 45° Ø110	ГОСТ 32414-2013		выбор заказчика	шт	12		2 шт. на поворот
33	Тройник канализационный ПП 45° (врезки ветвей)	ГОСТ 32414-2013		выбор заказчика	шт	10		
34	Ревизия канализационная ПП (после поворота трассы)	ГОСТ 32414-2013		выбор заказчика	шт	8		доступ сохранить
35	Фитинги PP-R Ø20: тройники, угольники 90° (ветви и повороты B1, Т3)	ГОСТ 32415-2013		выбор заказчика	шт	44		
36	Водорозетка PP-R Ø20×½" настенная, с креплением	ГОСТ 32415-2013		выбор заказчика	шт	16		коды — лист выводов
37	Вывод в пол PP-R Ø20 под встраиваемую часть напольного смесителя (переход на ½" по паспорту смесителя)	ГОСТ 32415-2013		выбор заказчика	шт	2		C_01
	Узлы ввода, люки, короба							
38	Кран шаровой латунный Ду15 PN16 (отключение ввода)	аналог		выбор заказчика	шт	6		Ст В1-1, Ст Т3-1, Ст В1-2, Ст Т3-2, Ст В1-3, Ст Т3-3
39	Фильтр сетчатый косой Ду15	аналог		выбор заказчика	шт	6		
40	Счётчик воды крыльчатый Ду15 (ХВ, ГВ), с поверкой	аналог		выбор заказчика	шт	6		пломба УК
41	Клапан обратный Ду15	аналог		выбор заказчика	шт	6		
42	Люк ревизионный нажимной под плитку 300×400 мм	аналог		выбор заказчика	шт	3		к стоякам и арматуре
43	Звукоизоляция стояка К1 в коробе: рулонный звукоизоляционный материал ≥ 10 мм, обмотка стояка на высоту этажа	аналог		выбор заказчика	м	8,1		Ст К1-1, Ст К1-2, Ст К1-3 (кухня)
44	Короб К1 над полом: профиль ПН/ПС, ГКЛВ 12,5 мм под плитку	аналог		выбор заказчика	м	11,2		сечение — лист разводки

Примечания

1. Форма 1 ГОСТ 21.110-2013, ширины граф изменены по п. 4.1. «Аналог» — аналог по характеристикам: модели внести до черновых работ, привязки выводов сверить по паспортам.
2. Бытовая техника не входит (показана арматура подключения), мойка — в комплекте кухни (марка — модуля кухни, как у столяра). Длины труб — трасса листа разводки + подъёмы + 10 %.
3. Стояк К1 в коробе — звукоизоляция стояка в коробе без жёсткого контакта короба с трубой.
4. Расчёт систем водоснабжения и канализации, диаметры магистралей и подбор оборудования выполняет проектная организация.

					Проект: Квартира с кабинетом
	Лист	№ док.	Подпись	Дата	Спецификация сантехнического оборудования
Дизайнер	Кырлан А.С.			04.11.26	

Стадия	Лист	Листов
П	52	127

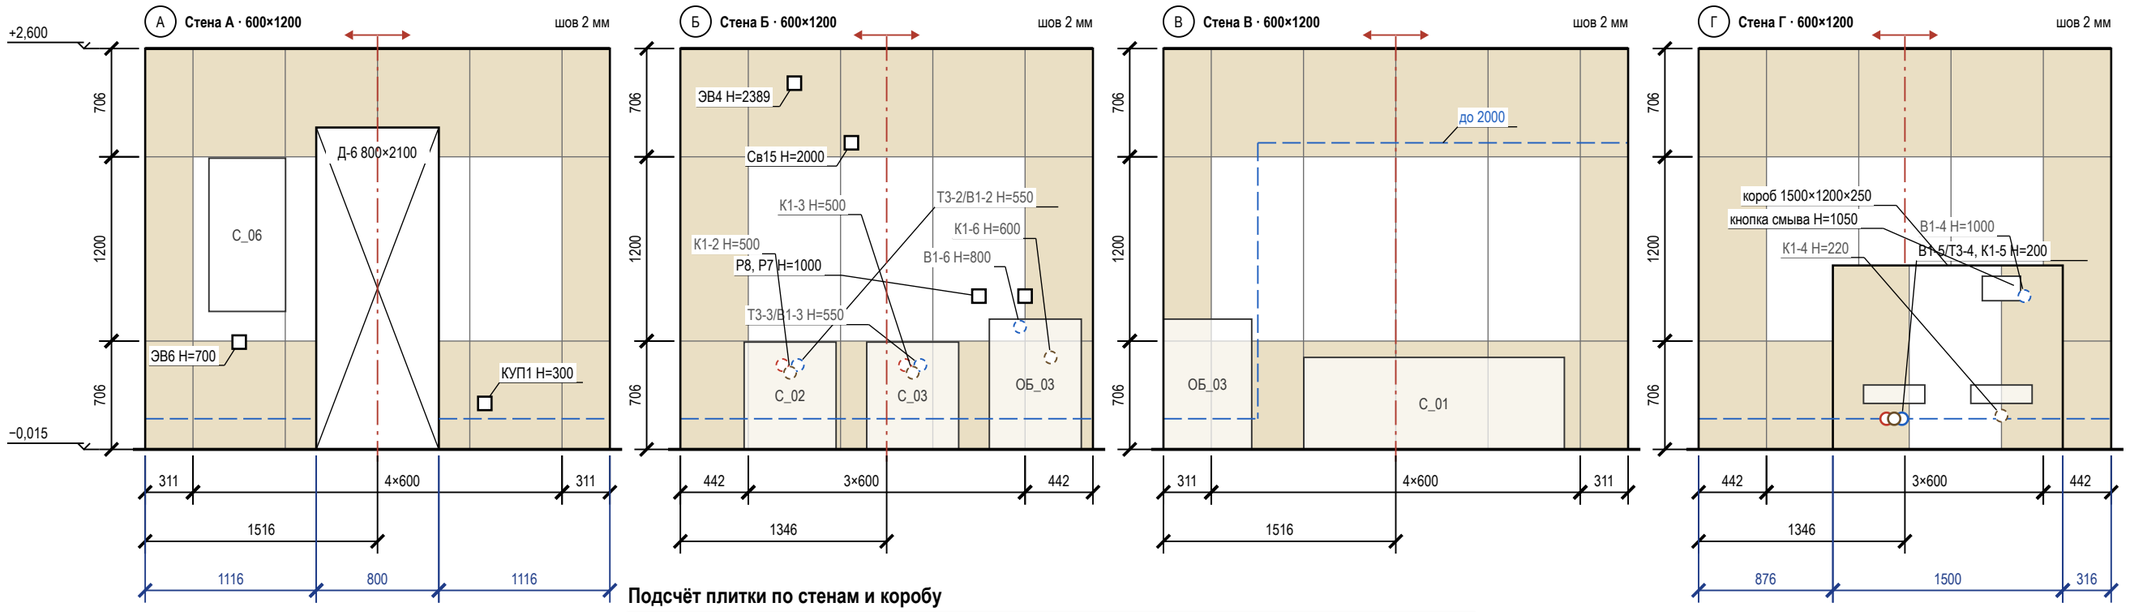

Условные обозначения

- плитка целая; тонкая линия — шов
- плитка с подрезкой (размер — на цепочке)
- ось старта; стрелки — направление укладки
- верх гидроизоляции: 200 от ЧП, в мокрой зоне — «до …»
- проём — не облицовывается
- сантехприбор: габарит, высота по практике
- короб инсталляции, в нём кнопка смыва 250×160
- вывод В1 (код — в ведомости привязок)
- вывод Т3 (код — в ведомости привязок)
- вывод К1 (код — в ведомости привязок)
- вывод за прибором / в коробе (не на сетке)
- электроточка: марка и Н — по листам ЭОМ
- отметка уровня, м: ±0,000 — чистый пол жилых помещений
- низ потолка; серая полоса — стена без плитки
- А — обозначение стены А–Г (как на развёртках)

Подсчёт плитки по стенам и коробу

Поверхность	L × H, мм	S, м²	Целых	Подр.	С запасом	Подрезки: край / верх, мм
стена А	3032 × 2615	6,37	2	16	20	311 / 311; 706
стена Б	2692 × 2615	7,17	3	12	17	442 / 442; 706
стена В	3032 × 2615	8,05	4	14	20	311 / 311; 706
стена Г	2692 × 2615	5,37	0	13	15	442 / 442; 706
короб (ст. Г)	1500×1200×250	2,77	1	7	9	лицо 399 / 600 / 497; бок. 250
Итого		**29,73**	**10**	**62**	**81**	


Сдвиг точек под раскладку

Точка (ВК, ЭОМ)	Стена	Проект: от угла / Н	Под раскладку: от угла / Н	Сдвиг, мм
КУП1	А	2216 / 300	2118 / 300	−98 на шов
Св15	Б	1116 / 2000	1045 / 2000	−71 на шов

Примечания

1. Вид изнутри, стены по часовой стрелке А → Г. Высоты — от чистого пола (−0,015), отметки — от ±0,000. Раскладка от чистовых размеров (штукатурка 10 + клей 5 + плитка 9 мм), подрезки чистые; старт от оси стены, ряды от середины (две подрезки).
2. Облицовка до потолка (+2,600).
3. Точки из таблицы сдвигов переносятся до черновой разводки (ЭОМ — по тем же числам).
4. Выводы ВК стоят по оси прибора и с прибором не двигаются — привязки по «Плану выводов сантехники» без сдвига; вне сетки (В1-5/Т3-4, К1-5) — отверстие в плитке коронкой по той же привязке, плитку не сдвигать.
5. За приборами и в коробе (Т3-2/В1-2, К1-2, Т3-3/В1-3, К1-3, В1-6, К1-6, В1-4, К1-4) — штриховым кольцом.
6. Гидроизоляция: 200 мм от ЧП по периметру; над ванной — до 2000 и 300 мм за борт (СП 29.13330.2011, п. 7.2 — на высоту замачивания); углы — лентой; акт скрытых работ, пролив.
7. Короб 1500×1200×250: лицо 399 / 600 / 497 мм от оси кнопки смыва, боковины, полка; углы — запил 45° или профиль; за коробом плитку не кладут.

					Проект: Квартира с кабинетом — **М 1:40**
	Лист	№ док.	Подпись	Дата	Раскладка плитки. Ванная. Развёртки стен
Дизайнер	Кырлан А.С.			04.11.26	Стадия: П · Лист: 53 · Листов: 127

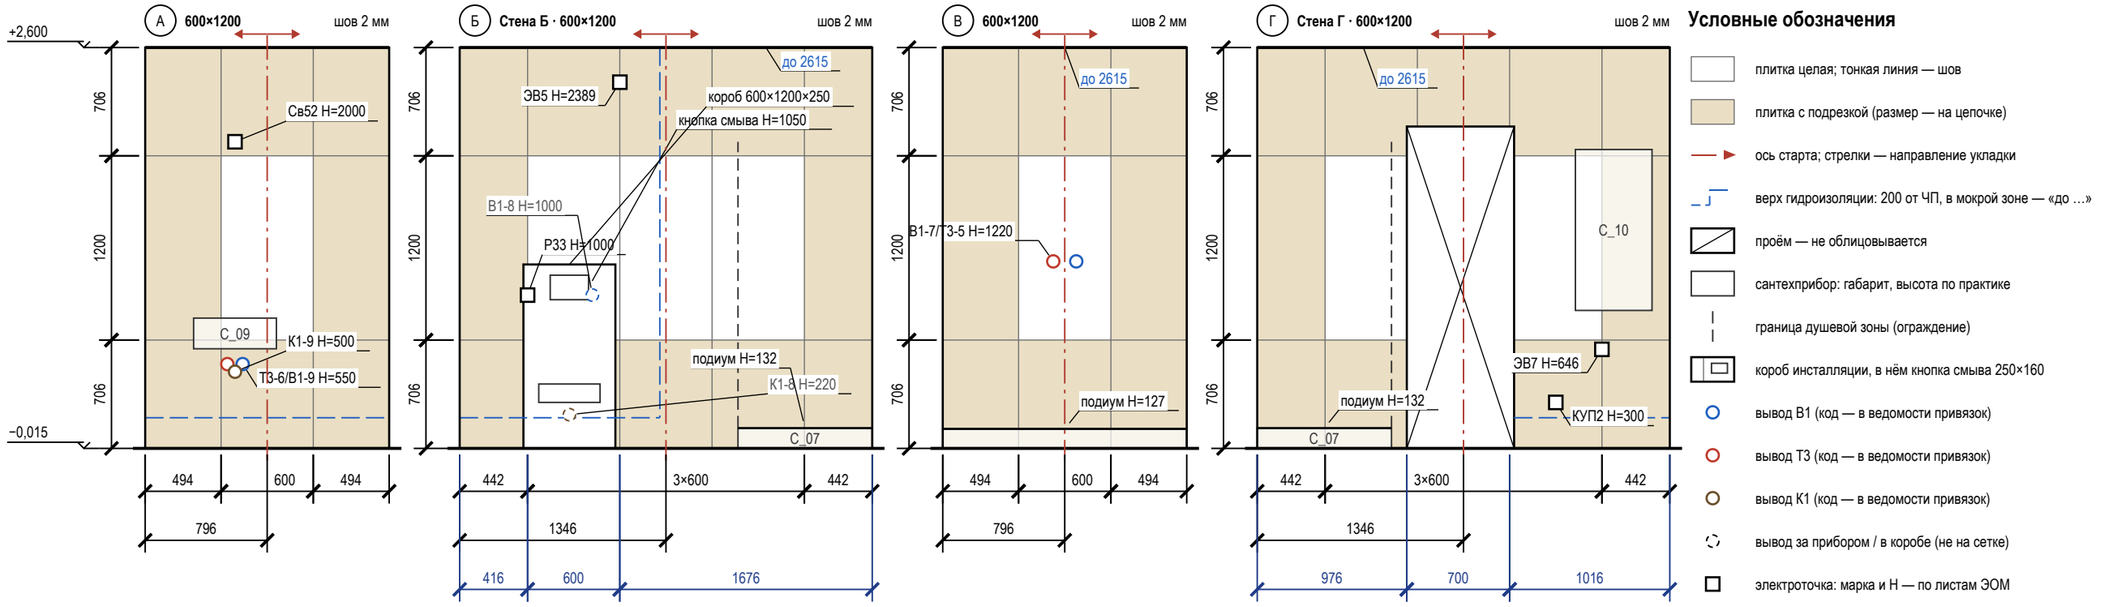

Условные обозначения

- плитка целая; тонкая линия — шов
- плитка с подрезкой (размер — на цепочке)
- ось старта; стрелки — направление укладки
- верх гидроизоляции: 200 от ЧП, в мокрой зоне — «до …»
- проём — не облицовывается
- сантехприбор: габарит, высота по практике
- граница душевой зоны (ограждение)
- короб инсталляции, в нём кнопка смыва 250×160
- вывод В1 (код — в ведомости привязок)
- вывод Т3 (код — в ведомости привязок)
- вывод К1 (код — в ведомости привязок)
- вывод за прибором / в коробе (не на сетке)
- электроточка: марка и Н — по листам ЭОМ
- отметка уровня, м: ±0,000 — чистый пол жилых помещений
- низ потолка; серая полоса — стена без плитки
- (А) обозначение стены А–Г (как на развёртках)

Подсчёт плитки по стенам и коробу

Поверхность	L × H, мм	S, м²	Целых	Подр.	С запасом	Подрезки: край / верх, мм
стена А	1592 × 2615	4,29	1	8	10	494 / 494; 706
стена Б	2692 × 2615	6,45	2	13	17	442 / 442; 706
короб (ст. Б)	600×1200×250	1,47	1	3	5	лицо 600; бок. 250
стена В	1592 × 2615	4,29	1	8	10	494 / 494; 706
стена Г	2692 × 2615	5,70	0	13	15	442 / 442; 706
Итого		**22,19**	**5**	**45**	**57**	


Сдвиг точек под раскладку

Точка (ВК, ЭОМ)	Стена	Проект: от угла / Н	Под раскладку: от угла / Н	Сдвиг, мм
Св52	А	586 / 2000	495 / 2000	−91 на шов

Примечания

1. Вид изнутри, стены по часовой стрелке А → Г. Высоты — от чистого пола (−0,015), отметки — от ±0,000. Раскладка от чистовых размеров (штукатурка 10 + клей 5 + плитка 9 мм), подрезки чистые; старт — от оси стены, ряды от середины (две подрезки).
2. Облицовка до потолка (+2,600).
3. Точки из таблицы сдвигов переносятся до черновой разводки (ЭОМ — по тем же числам).
4. Выводы ВК стоят по оси прибора и с прибором не двигаются — привязки по «Плану выводов сантехники» без сдвига; вне сетки (Т3-6/В1-9, К1-9) — отверстие в плитке коронкой по той же привязке, плитку не сдвигать.
5. За приборами и в коробе (В1-8, К1-8) — штриховым кольцом.
6. Подиум душа C_07: верх у решётки трапа +0,105 (h 120 мм), к стенам поднимается уклоном к трапу — «подиум Н=…» на развёртке — верх подиума у этой стены; облицовка стен в зоне душа — от верха подиума, грань ступени — плиткой пола. Выводы В1-7, Т3-5: Н=1220 от чистого пола помещения = 1100 от верха подиума у трапа.
7. Гидроизоляция: 200 мм от ЧП по периметру; у душа — на всю высоту стен душевой зоны и 500 мм за край душевой зоны (СП 29.13330.2011, п. 7.2 — на высоту замачивания); углы — лентой; акт скрытых работ, пролив.
8. Короб 600×1200×250: лицо 600 мм от оси кнопки смыва, боковины, полка; углы — запил 45° или профиль; за коробом плитку не кладут.

					Проект: Квартира с кабинетом	**М 1:40**
	Лист	№ док.	Подпись	Дата		
Дизайнер	Кырлан А.С.			04.11.26	Раскладка плитки. Санузел гостевой. Развёртки стен	Стадия: П; Лист: 54; Листов: 127

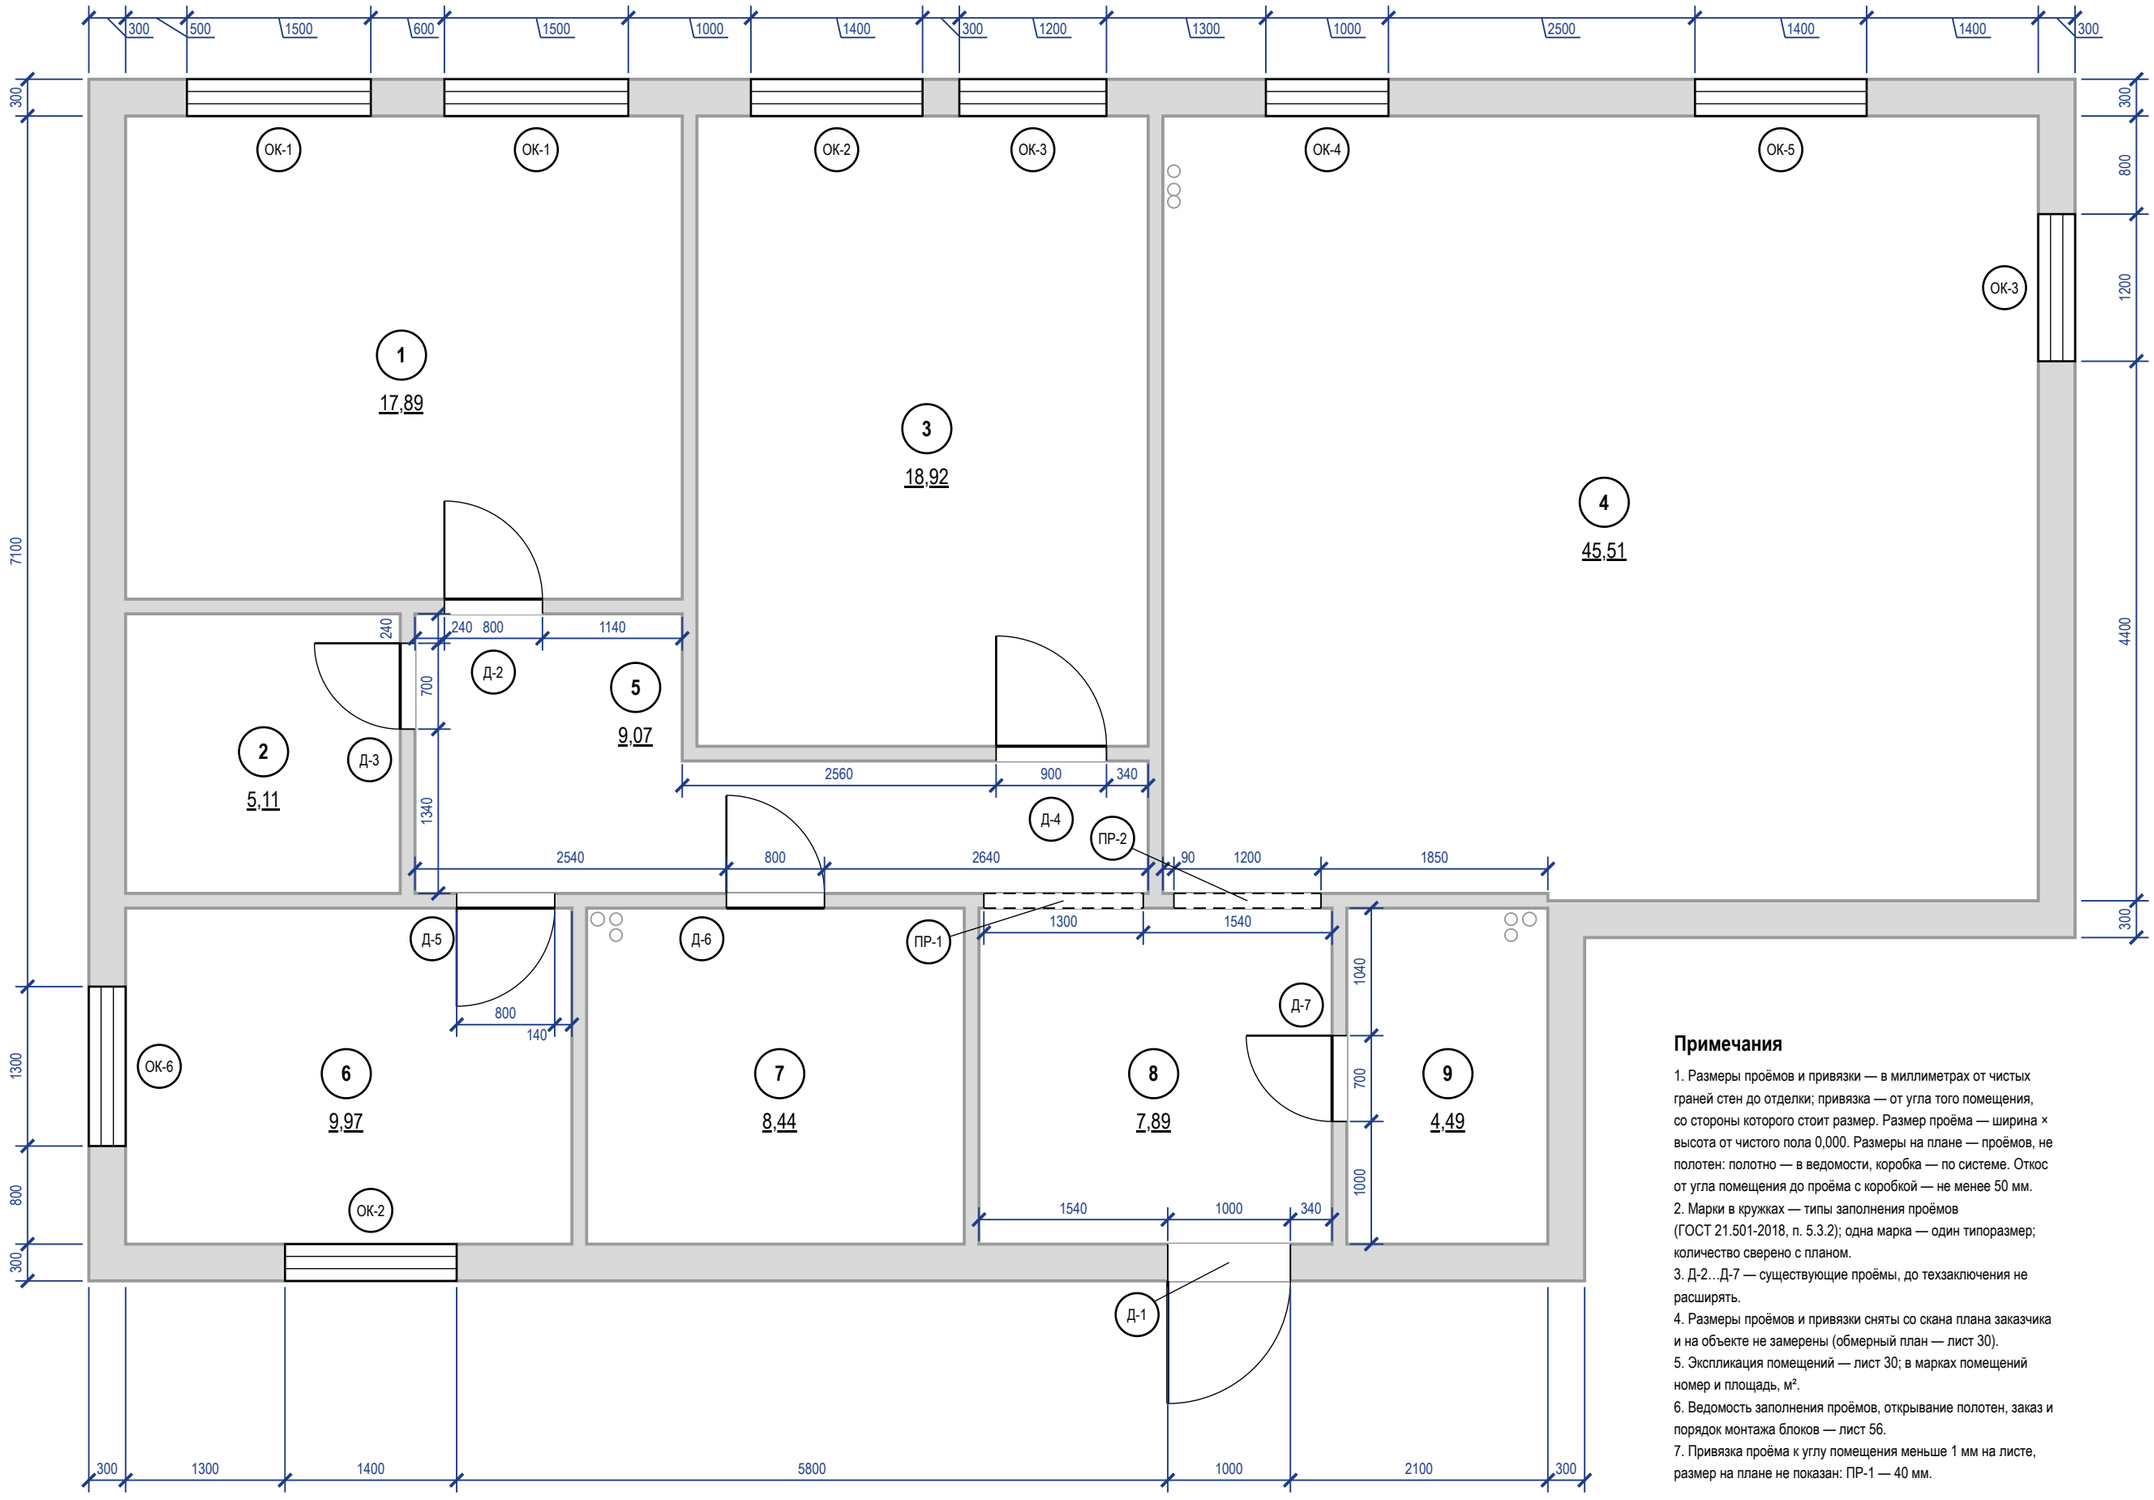

Примечания


1. Размеры проёмов и привязки — в миллиметрах от чистых граней стен до отделки; привязка — от угла того помещения, со стороны которого стоит размер. Размер проёма — ширина × высота от чистого пола 0,000. Размеры на плане — проёмов, не полотен: полотно — в ведомости, коробка — по системе. Откос от угла помещения до проёма с коробкой — не менее 50 мм.
2. Марки в кружках — типы заполнения проёмов (ГОСТ 21.501-2018, п. 5.3.2); одна марка — один типоразмер; количество сверено с планом.
3. Д-2…Д-7 — существующие проёмы, до техзаключения не расширять.
4. Размеры проёмов и привязки сняты со скана плана заказчика и на объекте не замерены (обмерный план — лист 30).
5. Экспликация помещений — лист 30; в марках помещений номер и площадь, м².
6. Ведомость заполнения проёмов, открывание полотен, заказ и порядок монтажа блоков — лист 56.
7. Привязка проёма к углу помещения меньше 1 мм на листе, размер на плане не показан: ПР-1 — 40 мм.

					Проект: Квартира с кабинетом	**М 1:50**
	Лист	№ док.	Подпись	Дата		
Дизайнер	Кырлан А.С.			04.11.26	План размещения дверей	Стадия: П; Лист: 55; Листов: 127

Ведомость заполнения проёмов

Марка	Наименование, обозначение	Проём ш×в, мм	Полотно (расч.)	Кол.	Откр.	Отделка полотна	Фурнитура	Прим.
Д-1	Блок дверной входной, ГОСТ 31173-2016	1000×2100	блок задать	1	Л	в комплекте блока	в комплекте блока (замки, глазок)	наружу
Д-2	Дверь скрытого монтажа, UNION FILO-60 Piatto	800×2100	700×2000	1	П	окраска No. 15 с двух сторон	скрытые петли 3D, магнитный замок	
Д-3	Дверь скрытого монтажа, UNION FILO-60 Piatto	700×2100	600×2000	1	Л	V503 — пом. 2, No. 15 — пом. 5	скрытые петли 3D, магнитный замок	
Д-4	Дверь скрытого монтажа, UNION FILO-60 Piatto	900×2100	800×2000	1	П	окраска No. 15 с двух сторон	скрытые петли 3D, магнитный замок	
Д-5	Дверь скрытого монтажа, UNION FILO-60 Piatto	800×2100	700×2000	1	Л	окраска No. 15 с двух сторон	скрытые петли 3D, магнитный замок	
Д-6	Дверь скрытого монтажа, UNION FILO-60 Piatto	800×2100	700×2000	1	П	в тон облицовки с двух сторон	скрытые петли 3D, магнитный замок, фиксатор WC	пом. 7; порог 15
Д-7	Дверь скрытого монтажа, UNION FILO-60 Piatto	700×2100	600×2000	1	Л	No. 15 — пом. 8, в тон облицовки — пом. 9	скрытые петли 3D, магнитный замок, фиксатор WC	порог 15
ПР-1	Портал без заполнения	1300×2100		1				б/п
ПР-2	Портал без заполнения	1200×2100		1				б/п
ОК-1	Блок оконный, ГОСТ 23166-2021	1500×1600		2				низ 800
ОК-2	Блок оконный, ГОСТ 23166-2021	1400×1600		2				низ 800
ОК-3	Блок оконный, ГОСТ 23166-2021	1200×1600		2				низ 800
ОК-4	Блок оконный, ГОСТ 23166-2021	1000×1400		1				низ 1000
ОК-5	Блок оконный, ГОСТ 23166-2021	1400×1600		1				низ 900
ОК-6	Блок оконный, ГОСТ 23166-2021	1300×1600		1				низ 800

Схемы дверных блоков (1:50) — вид со стороны открывания; вершина треугольника — сторона петель

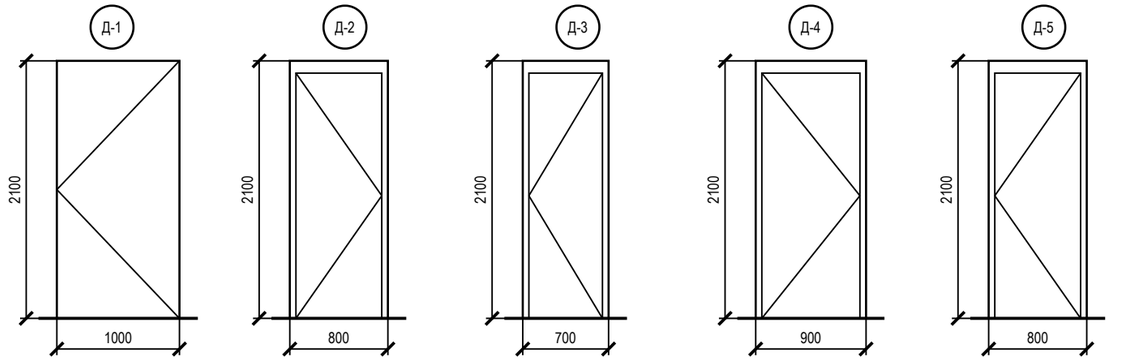


блок — по ГОСТ 31173 откр. Л

полотно 700×2000 (расч.) откр. П

полотно 600×2000 (расч.) откр. Л

полотно 800×2000 (расч.) откр. П

полотно 700×2000 (расч.) откр. Л

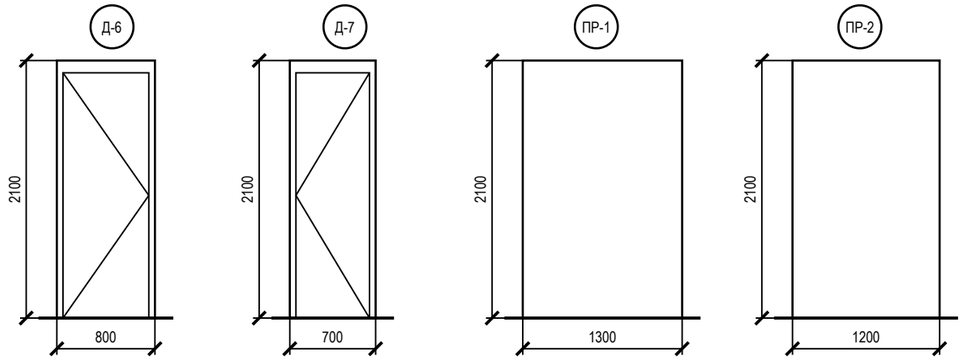

полотно 700×2000 (расч.) откр. П

полотно 600×2000 (расч.) откр. Л

без заполнения


без заполнения

Примечания

1. Марки проёмов — те же, что на плане размещения дверей (лист 55); привязки проёмов — там же.
2. Открывание: Л — петли слева, П — справа, если смотреть со стороны, куда открывается полотно (на себя).
3. Скрытые двери (Д-2…Д-7): проём замерить в чистоте; блок заказать до штукатурки (≈ 30 дн.), короб ставить до штукатурки; полотно навесить после чистовой отделки, красить в цвет стен. Порядок — практика монтажа, изготовитель подтверждает.
4. Полотно «расч.» — по проёму и ряду изделия с запасом по каталогам, заказ — по таблице проёмов модели; Д-2…Д-7: проём 2100, а под полотно 2000 по каталогам нужен 2050–2080, под 2100 — 2150–2180: высоту проёма — по модели; Д-1: входной блок по ГОСТ 31173-2016 — задать при выборе блока.

					Проект: Квартира с кабинетом
	Лист	№ док.	Подпись	Дата	
Дизайнер	Кырлан А.С.			04.11.26	Ведомость заполнения проёмов

Стадия	Лист	Листов
П	56	127

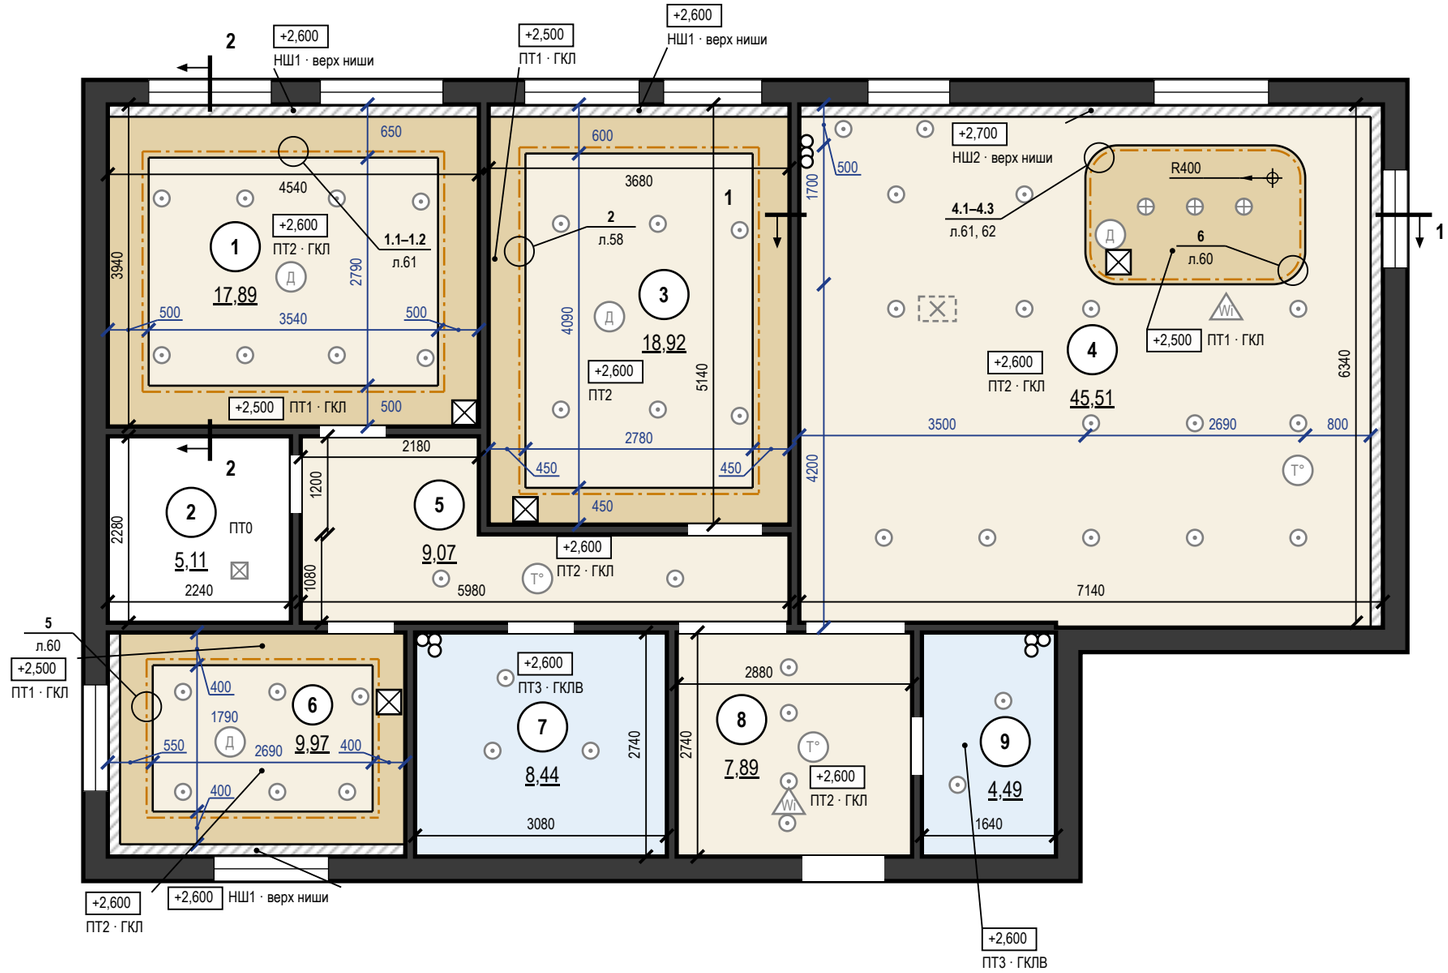

Ведомость потолков

Пом.	Марка	Конструкция	Низ / верх ниши	S, м²	Q
1	ПТ1	ГКЛ П113, короб LED	+2,500	7,33	Q3
1	ПТ2	ГКЛ П113	+2,600	9,88	Q3
1	НШ1	ниша под шторы 150×100	+2,600	0,68	
2	ПТ0	Существующий потолок, окраска	+2,700	5,11	
3	ПТ1	ГКЛ П113, короб LED	+2,500	7,00	Q3
3	ПТ2	ГКЛ П113	+2,600	11,37	Q3
3	НШ1	ниша под шторы 150×100	+2,600	0,55	
4	ПТ1	ГКЛ П113, остров + LED	+2,500	4,43	Q3
4	ПТ2	ГКЛ П113	+2,600	39,07	Q3
4	НШ2	ниша под шторы 150×100	+2,700	2,01	
5	ПТ2	ГКЛ П113	+2,600	9,07	Q3
6	ПТ1	ГКЛ П113, короб LED	+2,500	4,22	Q3
6	ПТ2	ГКЛ П113	+2,600	4,81	Q3
6	НШ1	ниша под шторы 150×100	+2,600	0,94	
7	ПТ3	ГКЛВ П113	+2,600	8,44	Q3
8	ПТ2	ГКЛ П113	+2,600	7,89	Q3
9	ПТ3	ГКЛВ П113	+2,600	4,49	Q3
		Итого		**127,29**	

Ведомость вырезов и закладных в потолке

Марка	Устройство	Кол.	Пом.
	Светильник встраиваемый (марки — план освещения)	47	1, 3, 4, 5, 6, 7, 8, 9
	Светильник накладной (марки — план освещения)	1	2
	Светильник подвесной (марки — план освещения)	3	4
ИП1, ИП2, ИП4, ИП7	Извещатель дымовой	4	1, 3, 4, 6
ИП5, ИП6, ИП3	Извещатель тепловой	3	4, 5, 8
AP2, AP1	Точка доступа Wi-Fi, PoE	2	4, 8
M_19	Вытяжка островная: закладная под подвес к плите, проход штанги и вывод питания через ГКЛ — по паспорту модели	1	4
	Люк ревизии 300×300	4	1, 3, 4, 6


Примечания

1. За отметку ±0,000 принят уровень чистого пола сухих помещений (готовое покрытие), а не существующего пола; пол пом. 7, 9 — −0,015; верх плиты перекрытия −0,064 — расчётный по пирогу пола, не замерен; существующий пол снимается до плиты, его отметка не замерена. Отметки в прямоугольниках — низ потолка; низ перекрытия +2,700. Марка потолка — одна конструкция и отметка на весь альбом.
2. Размеры помещений в свету (ширина × длина, мм), не поместившиеся на плане: пом. 4 — 7140 × 6340, 4000 × 60; пом. 6 — 3640 × 2740; пом. 9 — 1640 × 2740.
3. Потолки ГКЛ — каркасная система П113: подвесы через 1000 (с запасом: СП 163, табл. 14 — до 1100 при 0,15 кН/м²), несущие профили через 500, основные через 1200 мм; листы — поперёк несущих профилей. В помещениях 7, 9 — ГКЛВ на оцинкованном каркасе.
4. Нижний уровень — пояс-короб по периметру шириной 500, 450, 400 мм, верхний — поле внутри пояса: пом. 1, 3, 6.
5. LED-лента в алюминиевом профиле посередине карниза короба шириной 500, 450, 400 мм (узел 1 — пом. 1, лист 58; узел 2 — пом. 3, лист 58; узел 5 — пом. 6, лист 60); длина по плану: пом. 1 — 13,3 м (в плане освещения 13,3); пом. 3 — 14,3 м (в плане освещения 14,3); пом. 6 — 9,6 м (в плане освещения 9,6).
6. Ниши под шторы 150×100 мм — на всю длину стены с окном; карниз — на закладной до обшивки (узел 4 — пом. 1, 3, 6, лист 59; узел 3 — пом. 4, лист 58).
7. Светильники и потолочные устройства — подложка с планов освещения, слаботочных систем и вентиляции (положение — по ним); вырезы и закладные — по ведомости на листе, до обшивки; отверстия не совмещать с профилями, глубина корпуса светильника до 70 мм.
8. Разрезы 1–1, 2–2 — на листе 58; высоты мебели и дверных блоков сверены с низом потолка в разрезах; гибка бортов фигур и ленты ниш — там же; размеры фигурных уровней — фрагмент 1 (лист 59).
9. Шпаклевание ГКЛ и условия приёмки — Q3: рассеянный дневной свет, осмотр с 2 м; боковой свет не оценивается.
10. Люки ревизии 300×300 мм — по центру блоков питания LED (БП1, БП2, БП4, БП6; координаты — план освещения).
11. ПТ0 — пом. 2: существующий потолок, окраска, без подвесного потолка, низ +2,700; материал и цвет — по ведомости отделки.
12. Сечения потолков М 1:10: пом. 3 — 3.1, 3.2 (лист 61); пом. 6 — 6.1, 6.2 (лист 62).

					Проект: Квартира с кабинетом — **М 1:75**
	Лист	№ док.	Подпись	Дата	
Дизайнер	Кырлан А.С.			04.11.26	План потолков — Стадия: П; Лист: 57; Листов: 127


Разрез 1–1 (М 1:40)

Пом. 4 Кухня-гостиная; линия разреза — план потолков, лист 57

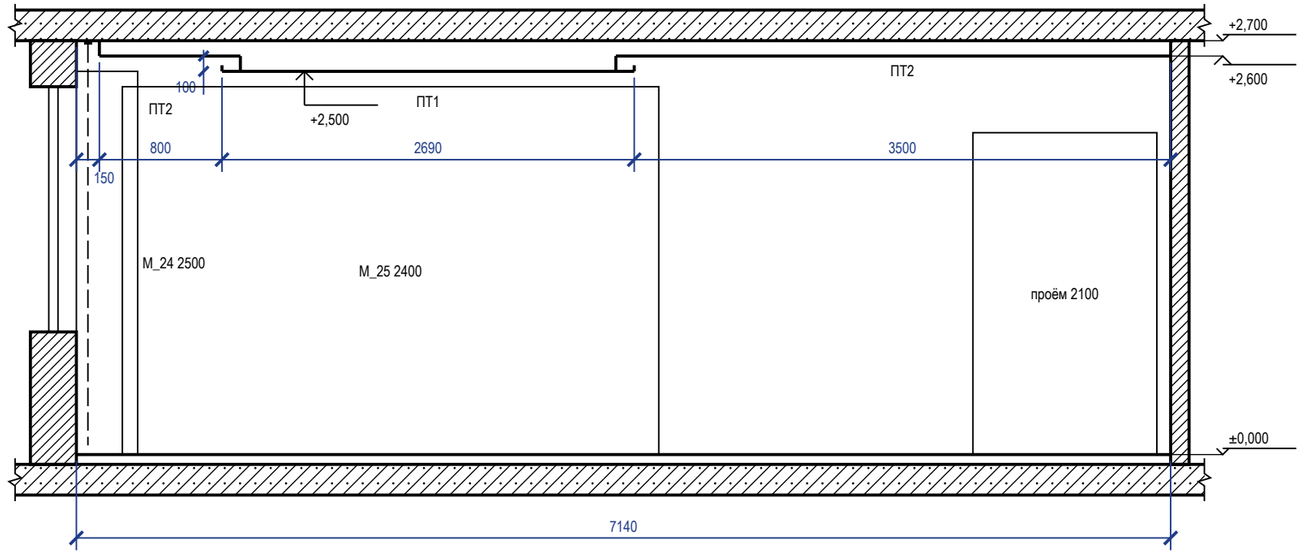

Разрез 2–2 (М 1:40)

Пом. 1 Спальня; линия разреза — план потолков, лист 57

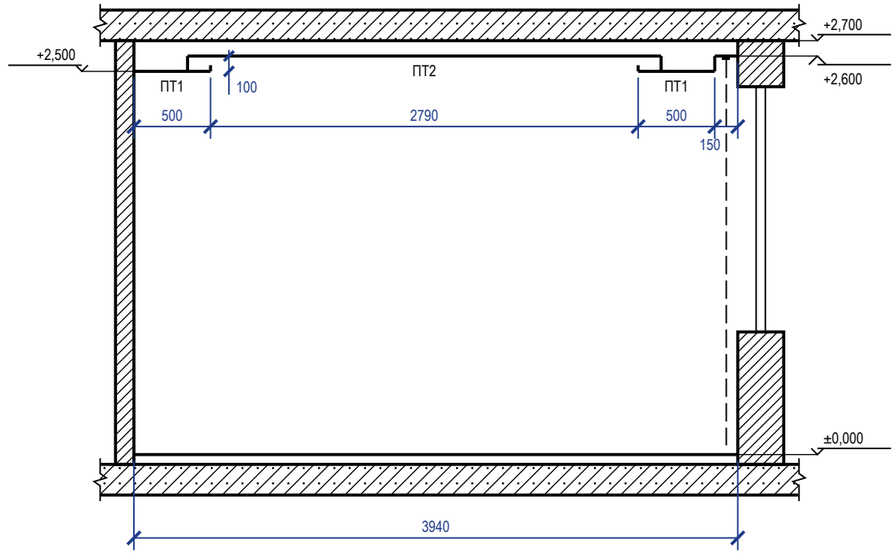

1 Короб с LED-подсветкой (М 1:10)

Пом. 1; карниз 150×100, щель под свет 60 мм

1 — плита перекрытия
2 — подвес прямой, шаг 1000 мм
3 — ПП 60×27: несущие через 500, основные через 1200 мм
4 — ГКЛ 12,5 по П113 — верхний уровень
5 — задняя стенка и бортик карниза — ГКЛ 12,5
6 — ПН 28×27 по периметру, к стене через 500 мм
7 — LED-лента в алюминиевом профиле
8 — низ короба — ГКЛ 12,5 по ПП 60×27

2 Короб с LED-подсветкой (М 1:10)

Пом. 3; карниз 150×100, щель под свет 60 мм


1 — плита перекрытия
2 — подвес прямой, шаг 1000 мм
3 — ПП 60×27: несущие через 500, основные через 1200 мм
4 — ГКЛ 12,5 по П113 — верхний уровень
5 — задняя стенка и бортик карниза — ГКЛ 12,5
6 — ПН 28×27 по периметру, к стене через 500 мм
7 — LED-лента в алюминиевом профиле
8 — низ короба — ГКЛ 12,5 по ПП 60×27

Условные обозначения

- плита перекрытия в сечении
- стена в сечении
- потолок ГКЛ в сечении; под линией — марка потолка (план потолков)
- мебель и дверные проёмы за секущей плоскостью; число — марка и верх от чистого пола, мм
- портьера в нише под шторы

3 Ниша под шторы (М 1:10)

Пом. 4; без подсветки; закладные под карниз — до обшивки

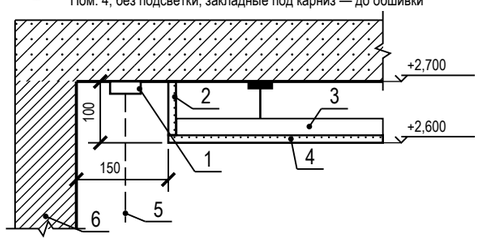

1 — карниз (шина), высота с верхом портьеры 80 мм
2 — стенка ниши — ГКЛ 12,5
3 — ПП 60×27 — каркас короба
4 — низ короба нижнего уровня — ГКЛ 12,5
5 — портьера
6 — стена с окном


Примечания

1. Разрезы — по линиям 1–1, 2–2 на плане потолков (лист 57). Отметки — от ±0,000 чистого пола, м; размеры — мм.
2. Высоты мебели и дверных блоков за секущей плоскостью сверены с низом потолка над ними: верх ниже низа короба и поля.
3. ГКЛ 12,5 мм по каркасу П113; перепад уровней и бортик карниза — ГКЛ по ПП 60×27 (узел 1 — на этом листе; узел 2 — на этом листе; узел 5 — лист 60). Ниша под шторы — на всю длину стены с окном, карниз на закладной до обшивки (узел 4 — лист 59; узел 3 — на этом листе).
4. Толщины плит перекрытия и пирога пола показаны условно.
5. Сечения потолков по помещениям М 1:10 (отметки помещения, профили, подвесы, крепёж, изделия) — листы 61–62.
6. Ведомость объёмов потолков (лист ГКЛ, профиль, подвесы, лента, блоки питания, люки) — на листе 59.
7. Фрагмент 1 — помещение с фигурными уровнями (размеры фигур, радиусы, отметки) — на листе 59.

					Проект: Квартира с кабинетом	М 1:40; 1:10
	Лист	№ док.	Подпись	Дата	Разрезы и узлы потолков	Стадия / Лист / Листов
Дизайнер	Кырлан А.С.			04.11.26		П / 58 / 127

Фрагмент 1. Пом. 4 Кухня-гостиная — уровни потолка (М 1:50)

Цепочки — от чистых граней стен; отметки — низ уровня от ±0,000

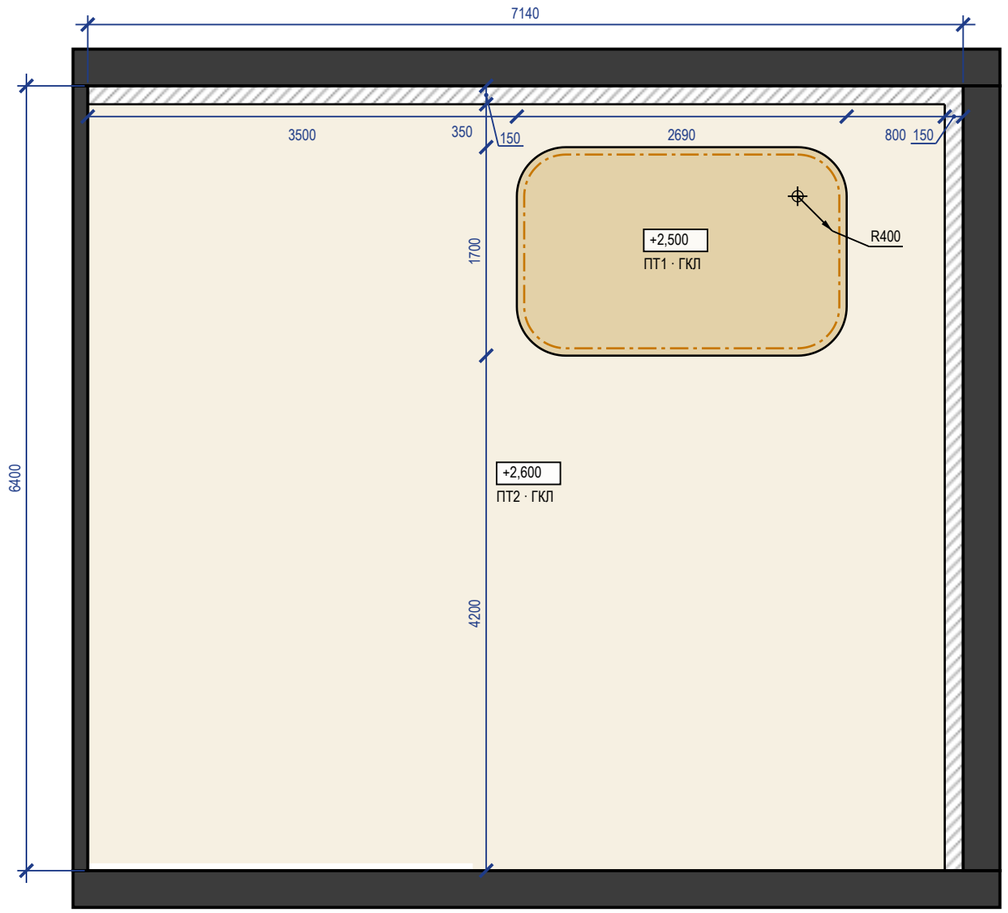


ПТ1 — низ +2,500 · ПТ2 — низ +2,600 · LED-лента в нише подсветки (карниз короба, ниша фигуры) · ниша под шторы

Ведомость объёмов потолков

Позиция	Ед.	Кол.	Пом.
Лист ГКЛ 12,5	м²	124,34	1, 3, 4, 5, 6, 8
Лист ГКЛВ 12,5	м²	12,93	7, 9
Лист ГКЛ арочный 6,5	м²	0,70	4
Борта и карнизы (входят в площади листов выше)	м²	15,46	1, 3, 4, 6
Профиль ПП 60×27	м	364,38	1, 3, 4, 5, 6, 7, 8, 9
Профиль ПН 28×27	м	309,84	1, 3, 4, 5, 6, 7, 8, 9
Подвес прямой	шт.	141	1, 3, 4, 5, 6, 7, 8, 9
Анкер-клин к плите	шт.	141	1, 3, 4, 5, 6, 7, 8, 9
Шуруп TN 3,5×25	шт.	3165	1, 3, 4, 5, 6, 7, 8, 9
Лента армирующая для швов	м	165,14	1, 3, 4, 5, 6, 7, 8, 9
Шпаклёвка для швов	кг	55,05	1, 3, 4, 5, 6, 7, 8, 9
Грунтовка (швы)	л	13,76	1, 3, 4, 5, 6, 7, 8, 9
Лента разделительная по периметру	м	122,60	1, 3, 4, 5, 6, 7, 8, 9
Сплошная шпаклёвка и окраска (площадь развёртки)	м²	137,62	1, 3, 4, 5, 6, 7, 8, 9
Лента LED	м	44,88	1, 3, 4, 6
Требуемая мощность блоков питания	Вт	560	1, 3, 4, 6
Установленная мощность блоков питания	Вт	900	1, 3, 4, 6
Блок питания LED	шт.	4	1, 3, 4, 6
Люк ревизии	шт.	4	1, 3, 4, 6

4 Ниша под шторы (М 1:10)

Пом. 1, 3, 6; без подсветки; закладные под карниз — до обшивки

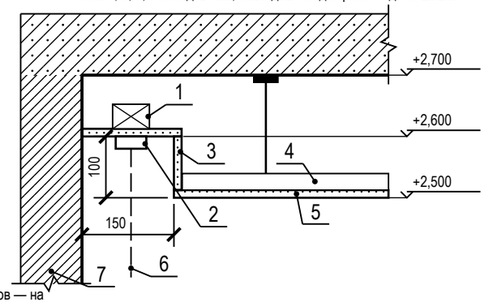

1 — закладная под карниз — брус 40×50
2 — карниз (шина), высота с верхом портьеры 80 мм
3 — стенка и потолок ниши — ГКЛ 12,5
4 — ПП 60×27 — каркас короба
5 — низ короба нижнего уровня — ГКЛ 12,5
6 — портьера
7 — стена с окном

Примечания

1. ГКЛ 12,5 мм по каркасу П113; узлы коробов и ниш под шторы: узел 1 — лист 58; узел 2 — лист 58; узел 5 — лист 60; узел 4 — на этом листе; узел 3 — лист 58; условные обозначения разрезов — на листе 58.
2. Фрагмент 1 (план потолков — лист 57) — фигурные уровни потолка крупно: привязки краёв и центров фигур к чистым граням стен, радиусы (R) с центрами, хорда и стрелка дуги, отметки низа каждого уровня; цвета уровней — как на плане потолков.
3. Фигурные уровни: борт — ГКЛ по ПН с надрезами (на дуге шаг стоек борта 300 мм при R до 2500, 400 — до 5000) или по гнутому заводскому профилю (СП 163, 6.3.3); гибка: остров пом. 4 R400 — ГКЛ 6,5 мокрой гибкой (СП 163, табл. 9). Лента в нише фигуры по оси: остров пом. 4 — 7,7 м; узел ниши LED фигуры: узел 6 — лист 60 — пом. 4.
4. Ведомость объёмов — по геометрии плана потолков: Лист ГКЛ 12,5 — плоскости уровней + борта (без арочных участков); Лист ГКЛВ 12,5 — плоскости уровней + борта; Лист ГКЛ арочный 6,5 — кривая борта × высота борта и стенки ниши × 2 слоя (R400 мокрая гибка); Борта и карнизы — длина перепада × перепад; Профиль ПП 60×27 — S × (1/шаг несущ. + 1/шаг осн.) + стойки бортов; Профиль ПН 28×27 — периметр стен + 2 × перепады + карнизы; Подвес прямой — по раскладке: S уровня / (шаг осн. × шаг подвесов), пояс уже шага — ряд вдоль пояса, фигура — по контуру; шаг подвесов — не больше табл. 14 СП 163; Анкер-клин к плите — по одному на подвес (Knauf П113); Шуруп TN 3,5×25 — 23 шт./м² (Knauf П113, табл. 2 альбома П 11); Лента армирующая для швов — 1,2 м/м² листа (Knauf); Шпаклёвка для швов — 0,4 кг/м² листа, только швы (Knauf); Грунтовка (швы) — 0,1 л/м² листа, только швы (Knauf); Лента разделительная по периметру — периметр стен под потолком ГКЛ; Сплошная шпаклёвка и окраска (площадь развёртки) — плоскости + борта; расход — по паспорту материала (норма расхода на сплошной слой не подтверждена); Лента LED — по оси карниза и ниши фигуры (план потолков); Требуемая мощность блоков питания — Вт/м × длина × 1,3; Установленная мощность блоков питания — сумма мощностей блоков по плану освещения; Блок питания LED блоки потолочных лент по плану освещения (БП1, БП2, БП4, БП6); Люк ревизии — план потолков; без запаса на подрезку (при закупке листа: ×1,075 при S > 20 м², ×1,175 — 10–20 м², ×1,275 — < 10 м²).

	Лист	№ док.	Подпись	Дата
Дизайнер	Кырлан А.С.			04.11.26


Проект: Квартира с кабинетом — **М 1:50; 1:10**

Разрезы и узлы потолков (продолжение)

Стадия	Лист	Листов
П	59	127

5 Короб с LED-подсветкой (М 1:10)


Пом. 6; карниз 150×100, щель под свет 60 мм

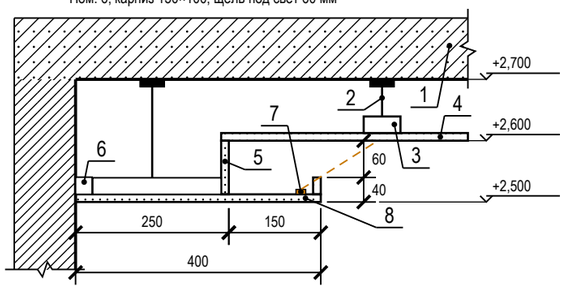

1 — плита перекрытия
2 — подвес прямой, шаг 1000 мм
3 — ПП 60×27: несущие через 500, основные через 1200 мм
4 — ГКЛ 12,5 по П113 — верхний уровень
5 — задняя стенка и бортик карниза — ГКЛ 12,5
6 — ПН 28×27 по периметру, к стене через 500 мм
7 — LED-лента в алюминиевом профиле
8 — низ короба — ГКЛ 12,5 по ПП 60×27

6 Ниша LED фигурного уровня (М 1:10)

Пом. 4; карниз 120×100, щель под свет 60 мм

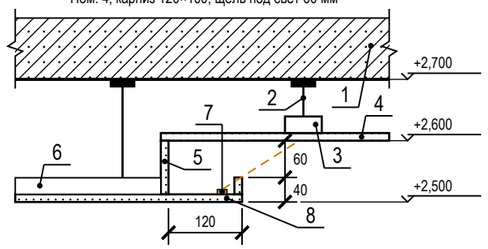

1 — плита перекрытия
2 — подвес прямой, шаг 1000 мм
3 — ПП 60×27: несущие через 500, основные через 1200 мм
4 — ГКЛ 12,5 по П113 — верхний уровень
5 — задняя стенка и бортик карниза — ГКЛ 12,5
6 — ПП 60×27 каркаса нижнего уровня, ПН по контуру фигуры (на дуге — с надрезами)
7 — LED-лента в алюминиевом профиле
8 — низ короба — ГКЛ 12,5 по ПП 60×27

Условные обозначения

— · — LED-лента в нише подсветки (карниз короба, ниша фигуры)


Примечания

1. ГКЛ 12,5 мм по каркасу П113; узлы коробов и ниш под шторы: узел 1 — лист 58; узел 2 — лист 58; узел 5 — на этом листе; узел 4 — лист 59; узел 3 — лист 58.

					Проект: Квартира с кабинетом	М 1:10
	Лист	№ док.	Подпись	Дата		
Дизайнер	Кырлан А.С.			04.11.26	Разрезы и узлы потолков (продолжение)	Стадия: П; Лист: 60; Листов: 127

Сечение 1.1. Короб с LED-подсветкой (М 1:10)


Пом. 1 Спальня; карниз 150×100, щель под свет 60 мм

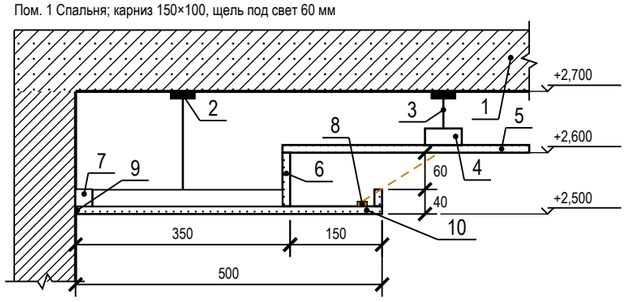

1 — плита перекрытия
2 — анкер-клин к плите — по одному на подвес
3 — подвес прямой, шаг 1000 мм
4 — ПП 60×27: несущие через 500, основные через 1200 мм; соединители одноуровневые, шурупы LN 3,5×9
5 — ГКЛ 12,5 по П113 — верхний уровень; шурупы TN 3,5×25 через 170 мм
6 — задняя стенка и бортик карниза — ГКЛ 12,5
7 — ПН 28×27 по периметру — дюбель-гвоздь через ≤ 500 мм, не менее 3 на профиль
8 — LED-лента 9,6 Вт/м, 24 В в алюминиевом профиле
9 — примыкание к стене — лента разделительная, шов зашпаклёван
10 — низ короба — ГКЛ 12,5 по ПП 60×27

Сечение 1.2. Ниша под шторы (М 1:10)


Пом. 1 Спальня; без подсветки; закладные под карниз — до обшивки

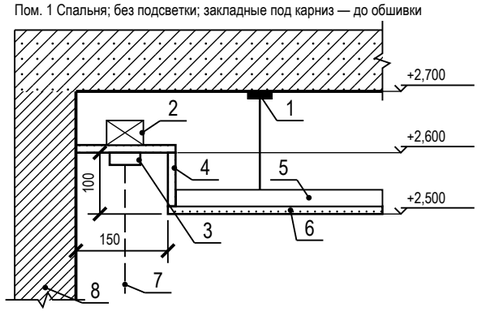

1 — анкер-клин к плите — по одному на подвес; подвес прямой, шаг 1000 мм
2 — закладная под карниз — брус 40×50
3 — карниз (шина), высота с верхом портьеры 80 мм
4 — стенка и потолок ниши — ГКЛ 12,5
5 — ПП 60×27 — каркас короба, основные через 1200 мм; соединители одноуровневые, шурупы LN 3,5×9
6 — низ короба нижнего уровня — ГКЛ 12,5; шурупы TN 3,5×25 через 170 мм
7 — портьера
8 — стена с окном

Сечение 3.1. Короб с LED-подсветкой (М 1:10)


Пом. 3 Кабинет; карниз 150×100, щель под свет 60 мм

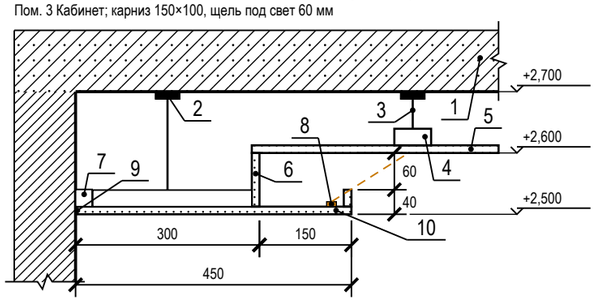

1 — плита перекрытия
2 — анкер-клин к плите — по одному на подвес
3 — подвес прямой, шаг 1000 мм
4 — ПП 60×27: несущие через 500, основные через 1200 мм; соединители одноуровневые, шурупы LN 3,5×9
5 — ГКЛ 12,5 по П113 — верхний уровень; шурупы TN 3,5×25 через 170 мм
6 — задняя стенка и бортик карниза — ГКЛ 12,5
7 — ПН 28×27 по периметру — дюбель-гвоздь через ≤ 500 мм, не менее 3 на профиль
8 — LED-лента 9,6 Вт/м, 24 В в алюминиевом профиле
9 — примыкание к стене — лента разделительная, шов зашпаклёван
10 — низ короба — ГКЛ 12,5 по ПП 60×27

Сечение 3.2. Ниша под шторы (М 1:10)


Пом. 3 Кабинет; без подсветки; закладные под карниз — до обшивки

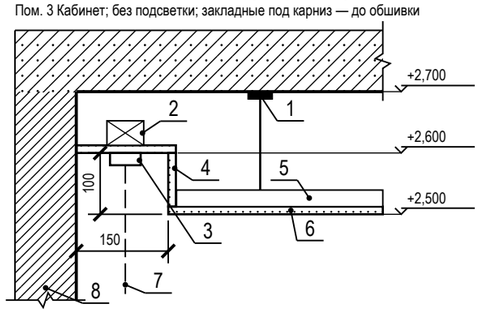

1 — анкер-клин к плите — по одному на подвес; подвес прямой, шаг 1000 мм
2 — закладная под карниз — брус 40×50
3 — карниз (шина), высота с верхом портьеры 80 мм
4 — стенка и потолок ниши — ГКЛ 12,5
5 — ПП 60×27 — каркас короба, основные через 1200 мм; соединители одноуровневые, шурупы LN 3,5×9
6 — низ короба нижнего уровня — ГКЛ 12,5; шурупы TN 3,5×25 через 170 мм
7 — портьера
8 — стена с окном

Сечение 4.1. Ниша LED фигурного уровня (М 1:10)


Пом. 4 Кухня-гостиная; карниз 120×100, щель под свет 60 мм

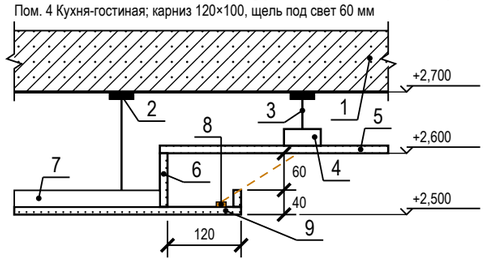

1 — плита перекрытия
2 — анкер-клин к плите — по одному на подвес
3 — подвес прямой, шаг 1000 мм
4 — ПП 60×27: несущие через 500, основные через 1200 мм; соединители одноуровневые, шурупы LN 3,5×9
5 — ГКЛ 12,5 по П113 — верхний уровень; шурупы TN 3,5×25 через 170 мм
6 — задняя стенка и бортик карниза — ГКЛ 12,5
7 — ПП 60×27 каркаса нижнего уровня, ПН по контуру фигуры (на дуге — с надрезами)
8 — LED-лента 9,6 Вт/м, 24 В в алюминиевом профиле
9 — низ короба — ГКЛ 12,5 по ПП 60×27

Сечение 4.2. Ниша под шторы (М 1:10)

Пом. 4 Кухня-гостиная; без подсветки; закладные под карниз — до обшивки

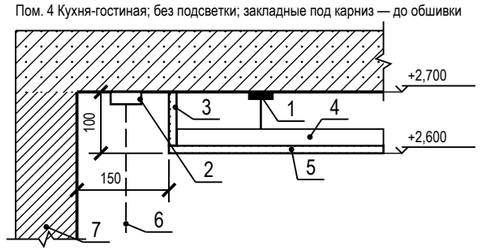

1 — анкер-клин к плите — по одному на подвес; подвес прямой, шаг 1000 мм
2 — карниз (шина), высота с верхом портьеры 80 мм
3 — стенка ниши — ГКЛ 12,5
4 — ПП 60×27 — каркас короба, основные через 1200 мм; соединители одноуровневые, шурупы LN 3,5×9
5 — низ короба нижнего уровня — ГКЛ 12,5; шурупы TN 3,5×25 через 170 мм
6 — портьера
7 — стена с окном

Условные обозначения

— · — LED-лента в нише подсветки (карниз короба, ниша фигуры)

Примечания

1. Сечения потолков М 1:10 по помещениям с нишами LED и нишами под шторы: отметки и размеры этого помещения от ±0,000 чистого пола (м, мм). Положение — по плану потолков (лист 57): короб и ниша LED — по линиям ленты, ниша под шторы — у стены с окном; типовые узлы по группам помещений — на листе 58.
2. Крепёж: подвес прямой к плите на анкер-клине — по одному на подвес (Knauf П113); ПН к стенам — дюбель-гвоздь через ≤ 500 мм, не менее 3 на профиль (серия 1.045.9-2.08); лист 12,5 — шурупы TN 3,5×25 через 170 мм (СП 163, табл. 15); профили между собой — соединители одноуровневые, шурупы LN 3,5×9.
3. Изделие карниза, профиля LED и галтели подписано артикулом из данных; где артикул не выбран, сечение дано по габаритам из данных (ширина и глубина ниши, щель под свет), изделие подбирается по ним.

					Проект: Квартира с кабинетом	М 1:10
	Лист	№ док.	Подпись	Дата	Сечения потолков М 1:10	Стадия / Лист / Листов
Дизайнер	Кырлан А.С.			04.11.26		П / 61 / 127

Сечение 4.3. Примыкание потолка к стене (М 1:10)


Пом. 4 Кухня-гостиная; примыкание — разделительная лента



1 — плита перекрытия
2 — анкер-клин к плите — по одному на подвес
3 — подвес прямой, шаг 1000 мм
4 — ПН 28×27 по периметру — дюбель-гвоздь через ≤ 500 мм, не менее 3 на профиль
5 — ПП 60×27 несущий (вид) через 500 мм, в ПН
6 — ПП 60×27 основной (сечение) через 1200 мм; соединители одноуровневые, шурупы LN 3,5×9
7 — лента разделительная по стене, шов зашпаклёван
8 — ГКЛ 12,5 по П113; шурупы TN 3,5×25 через 170 мм

Сечение 6.1. Короб с LED-подсветкой (М 1:10)


Пом. 6 Детская; карниз 150×100, щель под свет 60 мм

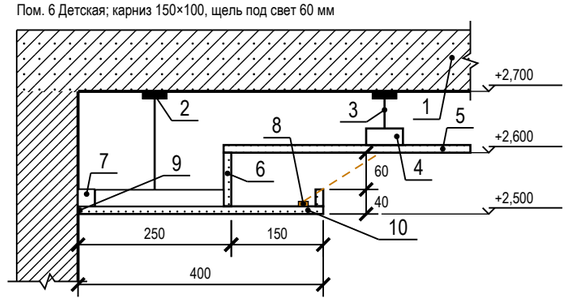

1 — плита перекрытия
2 — анкер-клин к плите — по одному на подвес
3 — подвес прямой, шаг 1000 мм
4 — ПП 60×27: несущие через 500, основные через 1200 мм; соединители одноуровневые, шурупы LN 3,5×9
5 — ГКЛ 12,5 по П113 — верхний уровень; шурупы TN 3,5×25 через 170 мм
6 — задняя стенка и бортик карниза — ГКЛ 12,5
7 — ПН 28×27 по периметру — дюбель-гвоздь через ≤ 500 мм, не менее 3 на профиль
8 — LED-лента 9,6 Вт/м, 24 В в алюминиевом профиле
9 — примыкание к стене — лента разделительная, шов зашпаклёван
10 — низ короба — ГКЛ 12,5 по ПП 60×27

Сечение 6.2. Ниша под шторы (М 1:10)

Пом. 6 Детская; без подсветки; закладные под карниз — до обшивки

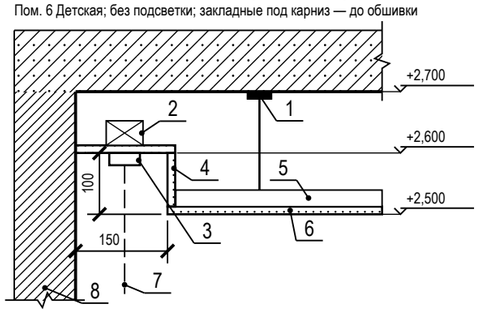

1 — анкер-клин к плите — по одному на подвес; подвес прямой, шаг 1000 мм
2 — закладная под карниз — брус 40×50
3 — карниз (шина), высота с верхом портьеры 80 мм
4 — стенка и потолок ниши — ГКЛ 12,5
5 — ПП 60×27 — каркас короба, основные через 1200 мм; соединители одноуровневые, шурупы LN 3,5×9
6 — низ короба нижнего уровня — ГКЛ 12,5; шурупы TN 3,5×25 через 170 мм
7 — портьера
8 — стена с окном

Условные обозначения


— · — LED-лента в нише подсветки (карниз короба, ниша фигуры)

Примечания

1. Сечения потолков М 1:10 по помещениям с нишами LED и нишами под шторы: отметки и размеры этого помещения от ±0,000 чистого пола (м, мм). Положение — по плану потолков (лист 57): короб и ниша LED — по линиям ленты, ниша под шторы — у стены с окном; типовые узлы по группам помещений — на листе 58.
2. Крепёж: подвес прямой к плите на анкер-клине — по одному на подвес (Knauf П113); ПН к стенам — дюбель-гвоздь через ≤ 500 мм, не менее 3 на профиль (серия 1.045.9-2.08); лист 12,5 — шурупы TN 3,5×25 через 170 мм (СП 163, табл. 15); профили между собой — соединители одноуровневые, шурупы LN 3,5×9.
3. Изделие карниза, профиля LED и галтели подписано артикулом из данных; где артикул не выбран, сечение дано по габаритам из данных (ширина и глубина ниши, щель под свет), изделие подбирается по ним.

					Проект: Квартира с кабинетом	М 1:10
	Лист	№ док.	Подпись	Дата		
Дизайнер	Кырлан А.С.			04.11.26	Сечения потолков М 1:10	Стадия: П; Лист: 62; Листов: 127

выпуск 04.11.2026 № 627e1ac6ce · стр. 62 из 127

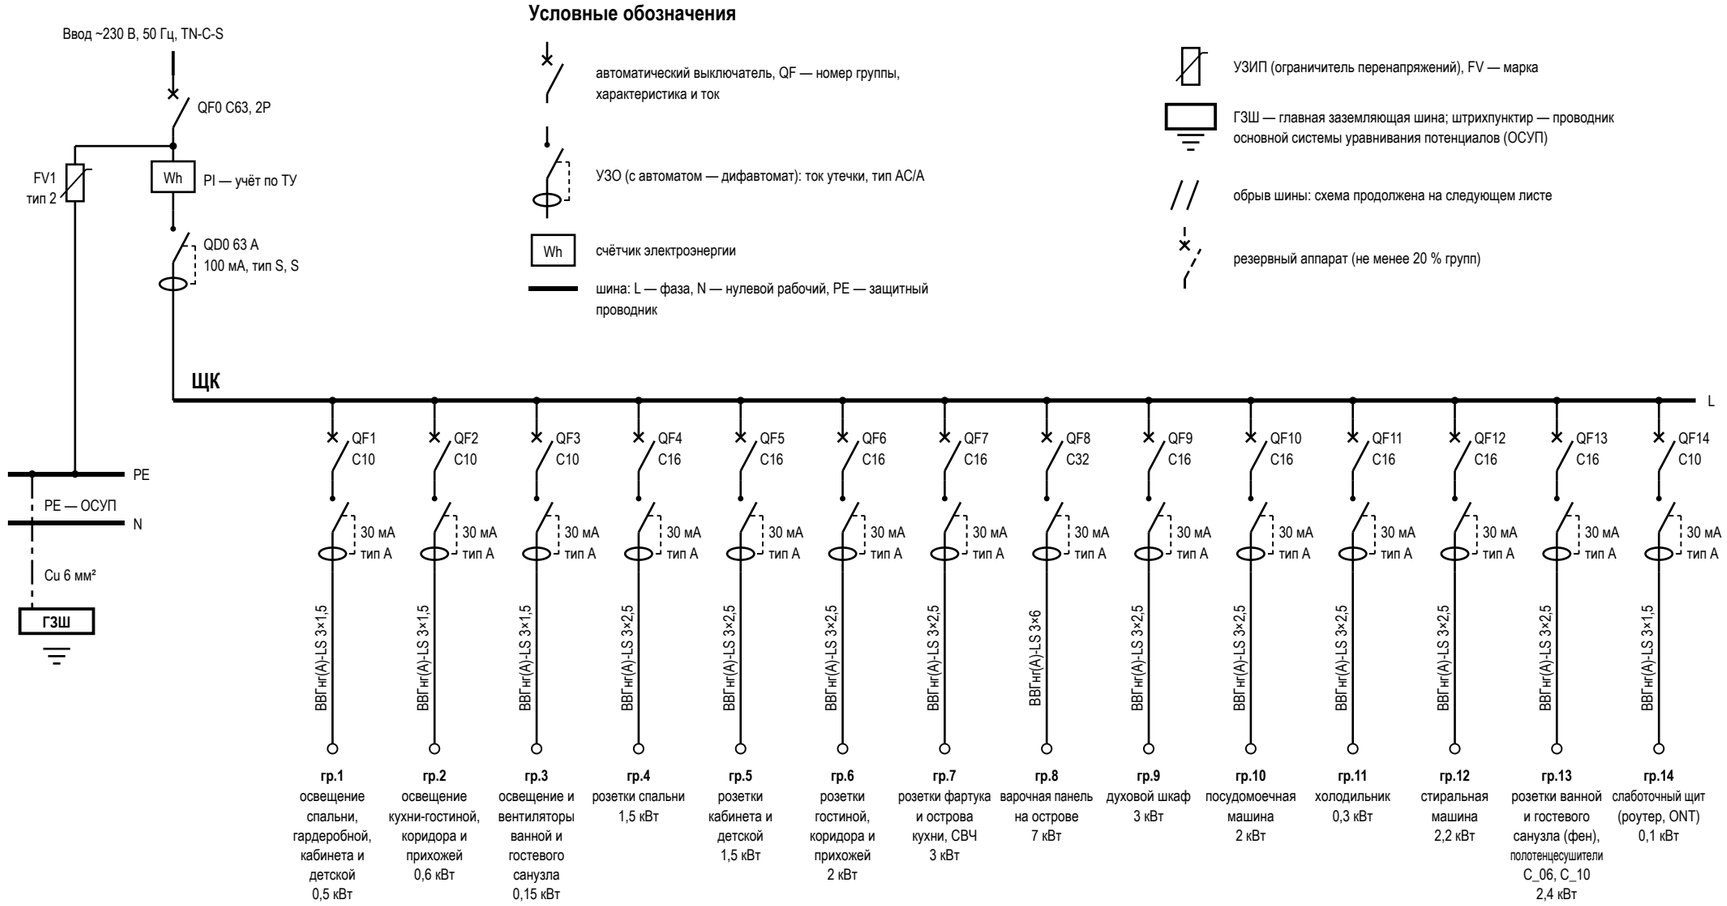

Условные обозначения

- автоматический выключатель, QF — номер группы, характеристика и ток
- УЗО (с автоматом — дифавтомат): ток утечки, тип AC/A
- Wh — счётчик электроэнергии
- шина: L — фаза, N — нулевой рабочий, PE — защитный проводник
- УЗИП (ограничитель перенапряжений), FV — марка
- ГЗШ — главная заземляющая шина; штрихпунктир — проводник основной системы уравнивания потенциалов (ОСУП)
- обрыв шины: схема продолжена на следующем листе
- резервный аппарат (не менее 20 % групп)

Данные щитка

Показатель	Значение
Номер щитка	ЩК
Тип	ЩРВ-П-48, IP41
Уст. мощность, кВт	26,25
Разреш. мощность, кВт	15
Расчётная, кВт	9,8
Автоматы 1п: занят. / рез.	14 / 3
Модулей: всего / занято	48 / 34
Ток на вводе, А	63
Вводной аппарат	QF0 C63, 2P
УЗИП	FV1, тип 2, ЩК, после счётчика
ГЗШ, проводник ОСУП	Cu 6 мм²
Листов схемы	2 (группы по листам)

Таблица групп щита ЩК и кабельный журнал


№	Назначение	Помещения	Автомат	УЗО / дифавтомат	Кабель	Длина, м	P, кВт	Точек
1	освещение спальни, гардеробной, кабинета и детской	1, 2, 3, 5, 6	C10	30 мА, тип A	ВВГнг(A)-LS 3×1,5	123,1	0,5	41
2	освещение кухни-гостиной, коридора и прихожей	4, 5, 8	C10	30 мА, тип A	ВВГнг(A)-LS 3×1,5	87	0,6	37
3	освещение и вентиляторы ванной и гостевого санузла	5, 7, 8, 9	C10	30 мА, тип A	ВВГнг(A)-LS 3×1,5	35	0,15	11
4	розетки спальни	1	C16	30 мА, тип A	ВВГнг(A)-LS 3×2,5	40,2	1,5	6
5	розетки кабинета и детской	3, 6	C16	30 мА, тип A	ВВГнг(A)-LS 3×2,5	44,8	1,5	10
6	розетки гостиной, коридора и прихожей	4, 5, 8	C16	30 мА, тип A	ВВГнг(A)-LS 3×2,5	49	2	8
7	розетки фартука и острова кухни, СВЧ	4	C16	30 мА, тип A	ВВГнг(A)-LS 3×2,5	30,7	3	5
8	варочная панель на острове	4	C32	30 мА, тип A	ВВГнг(A)-LS 3×6	12,4	7	1
9	духовой шкаф	4	C16	30 мА, тип A	ВВГнг(A)-LS 3×2,5	17,8	3	1
10	посудомоечная машина	4	C16	30 мА, тип A	ВВГнг(A)-LS 3×2,5	17,4	2	1
11	холодильник	4	C16	30 мА, тип A	ВВГнг(A)-LS 3×2,5	14,4	0,3	1
12	стиральная машина	7	C16	30 мА, тип A	ВВГнг(A)-LS 3×2,5	15,2	2,2	1
13	розетки ванной и гостевого санузла (фен), полотенцесушители C_06, C_10	7, 9	C16	30 мА, тип A	ВВГнг(A)-LS 3×2,5	31,2	2,4	4
14	слаботочный щит (роутер, ONT)	8	C10	30 мА, тип A	ВВГнг(A)-LS 3×1,5	3,5	0,1	1
	Итого по сечениям ВВГнг(A)-LS (все группы щита), м: 3×1,5 — 248,6; 3×2,5 — 260,7; 3×6 — 12,4					521,7		

Примечания

1. Схема однолинейная: одна линия — фаза, N и PE группы; аппараты — в отключённом положении (ГОСТ 2.702, ГОСТ 2.755). Номера групп — как у точек на планах (гр.). За отметку 0,000 принят уровень чистого пола; высота щита — по плану розеток.
2. Розеточные и мокрые линии — через УЗО или дифавтомат с током утечки не более 30 мА (ПУЭ 7.1.79); в санузле выполнить ДСУП (ПУЭ 7.1.87–7.1.88).
3. УЗО тип A — для линий с электроникой, стиральной и посудомоечной машиной, LED-драйверами; тип AC — только для чисто активной нагрузки.
4. Кабель — медный, исполнение нг(A)-LS (ГОСТ 31565-2012); скрытая прокладка только горизонтально и вертикально, фактические трассы зафиксировать исполнительной схемой до закрытия отделкой.
5. Номинал автомата — не выше допустимого тока кабеля: 1,5 мм² — до 10 А, 2,5 мм² — до 16 А. Резерв щита — не менее 20 % модулей.
6. Расчёт нагрузок, токов КЗ, селективности и сечений — по проекту ЭОМ организации с допуском СРО; лист задаёт состав, расположение и группы.
7. УЗИП FV1 — после вводного автомата, проводник к шине PE — кратчайший, без петель. Шина PE щита соединяется с ГЗШ проводником ОСУП; к ГЗШ присоединяются трубы водопровода и отопления на вводе в квартиру (ПУЭ 7.1.87). Шины N и PE — раздельные, после разделения PEN не объединяются.
8. До подключения нагрузки — приёмо-сдаточные испытания с протоколом: сопротивление изоляции линий не менее 0,5 МОм, срабатывание УЗО по току и времени, непрерывность защитных проводников PE (ПУЭ, гл. 1.8).

					Проект: Квартира с кабинетом
	Лист	№ док.	Подпись	Дата	
Дизайнер	Кырлан А.С.			04.11.26	Однолинейная схема щита
					Стадия: П; Лист: 63; Листов: 127


Продолжение однолинейной схемы щита ЩК, начало — лист 63

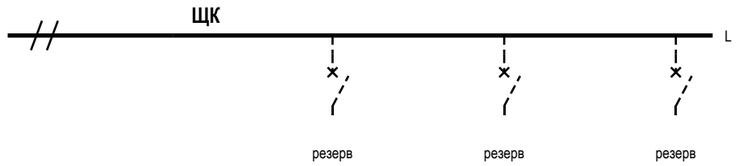

Примечания

1. Лист — продолжение однолинейной схемы щита ЩК: начало, данные щитка и условные обозначения — лист 63. Ввод, учёт, вводной аппарат, УЗИП, шины N и PE и ГЗШ показаны там же; шина L листа — та же шина щита.
2. Схема однолинейная: одна линия — фаза, N и PE группы; аппараты — в отключённом положении (ГОСТ 2.702, ГОСТ 2.755). Номера групп — как у точек на планах (гр.). За отметку 0,000 принят уровень чистого пола; высота щита — по плану розеток.
3. Розеточные и мокрые линии — через УЗО или дифавтомат с током утечки не более 30 мА (ПУЭ 7.1.79); в санузле выполнить ДСУП (ПУЭ 7.1.87–7.1.88).
4. УЗО тип A — для линий с электроникой, стиральной и посудомоечной машиной, LED-драйверами; тип AC — только для чисто активной нагрузки.
5. Кабель — медный, исполнение нг(A)-LS (ГОСТ 31565-2012); скрытая прокладка только горизонтально и вертикально, фактические трассы зафиксировать исполнительной схемой до закрытия отделкой.
6. Номинал автомата — не выше допустимого тока кабеля: 1,5 мм² — до 10 А, 2,5 мм² — до 16 А. Резерв щита — не менее 20 % модулей.
7. Расчёт нагрузок, токов КЗ, селективности и сечений — по проекту ЭОМ организации с допуском СРО; лист задаёт состав, расположение и группы.
8. До подключения нагрузки — приёмо-сдаточные испытания с протоколом: сопротивление изоляции линий не менее 0,5 МОм, срабатывание УЗО по току и времени, непрерывность защитных проводников PE (ПУЭ, гл. 1.8).

					Проект: Квартира с кабинетом		
	Лист	№ док.	Подпись	Дата	Однолинейная схема щита (продолжение)	Стадия	Лист	Листов
Дизайнер	Кырлан А.С.			04.11.26		П	64	127

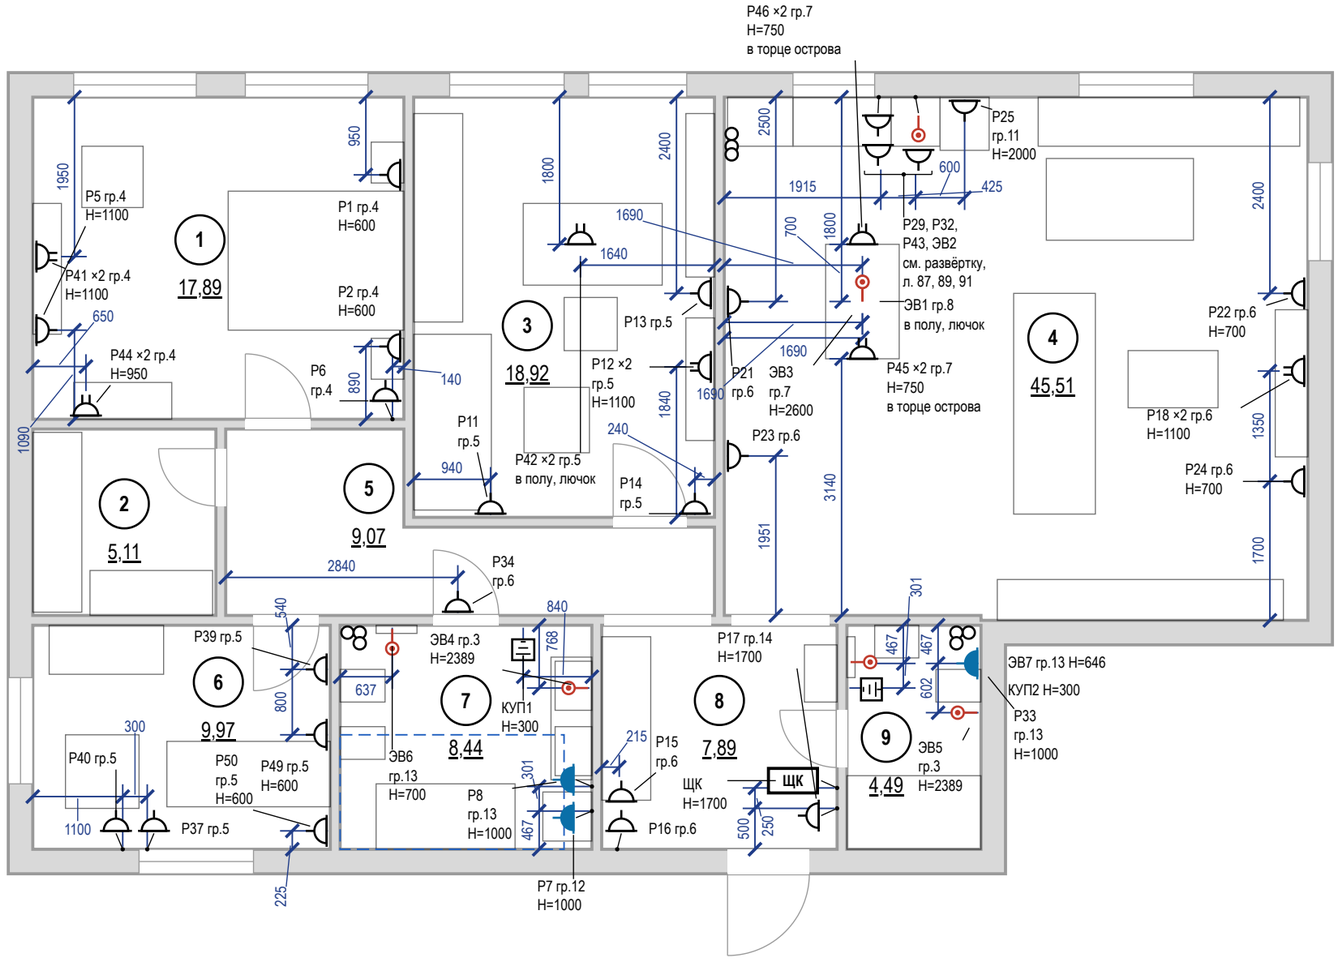

Условные обозначения

Знак	Тип изделия	Н, мм	Кол., шт
	Розетка с заземлением	300	13
	То же	у знака	11
	Блок розеток с заземлением, рамка 2 поста	у знака	7
	Розетка с заземлением IP44	1000	3
	Вывод кабеля к прибору	у знака	7
	КУП (уравнивание потенциалов)	300	2
ЩК	Щит квартирный	1700	1

розетка с заземляющим контактом; у знака — марка, ×N — постов в рамке, гр. — группа щита, Н — высота оси, мм

знак разведён для читаемости: точка на стене — у выноски, привязка — до неё

граница зоны 2 ванной (600 мм от ванны/поддона)

мебель и сантехприборы — подложка

стояк: К1 — канализация, В1 — ХВС, Т3 — ГВС


1 — номер помещения, площадь м²

Итого розеток (механизмов) — 41 шт; рамок — 34 шт: на 1 пост — 27, на 2 поста — 7.

Примечания

1. За отметку 0,000 принят уровень чистого пола. Высоты Н — от чистого пола до оси изделия; привязки — от чистовой грани стены до оси механизма (у рамки на несколько постов — до оси рамки).
2. Розетки без отметки Н у знака — на высоте 300 мм от чистого пола до оси механизма; выводы кабеля — по паспорту прибора.
3. Розетки в санузле — только вне зон 0–2 (ПУЭ 7.1.48, ГОСТ Р 50571.7.701-2024), IP44, через УЗО 30 мА.
4. Розеточные и мокрые линии — через УЗО или дифавтомат с током утечки не более 30 мА (ПУЭ 7.1.79); в санузле выполнить ДСУП (ПУЭ 7.1.87–7.1.88).
5. Кабель — медный, исполнение нг(А)-LS (ГОСТ 31565-2012); скрытая прокладка только горизонтально и вертикально, фактические трассы зафиксировать исполнительной схемой до закрытия отделкой.
6. Расчёт нагрузок, токов КЗ, селективности и сечений — по проекту ЭОМ организации с допуском СРО; лист задаёт состав, расположение и группы.
7. Выводы кухонной техники — после утверждения проекта кухни (ориентировочно); привязки выводов даны от осей модулей гарнитура и пересматриваются вместе с проектом кухни.
8. Электрический тёплый пол проектом не предусмотрен; при решении заказчика устроить — отдельный лист «План тёплых полов»: контуры с отступом 100 мм от стен и мебели без ножек, датчик в гофре, терморегулятор, своя группа щита через УЗО 30 мА.

					Проект: Квартира с кабинетом	М 1:75
	Лист	№ док.	Подпись	Дата		
Дизайнер	Кырлан А.С.			04.11.26	План розеток и электровыводов	Стадия: П; Лист: 65; Листов: 127

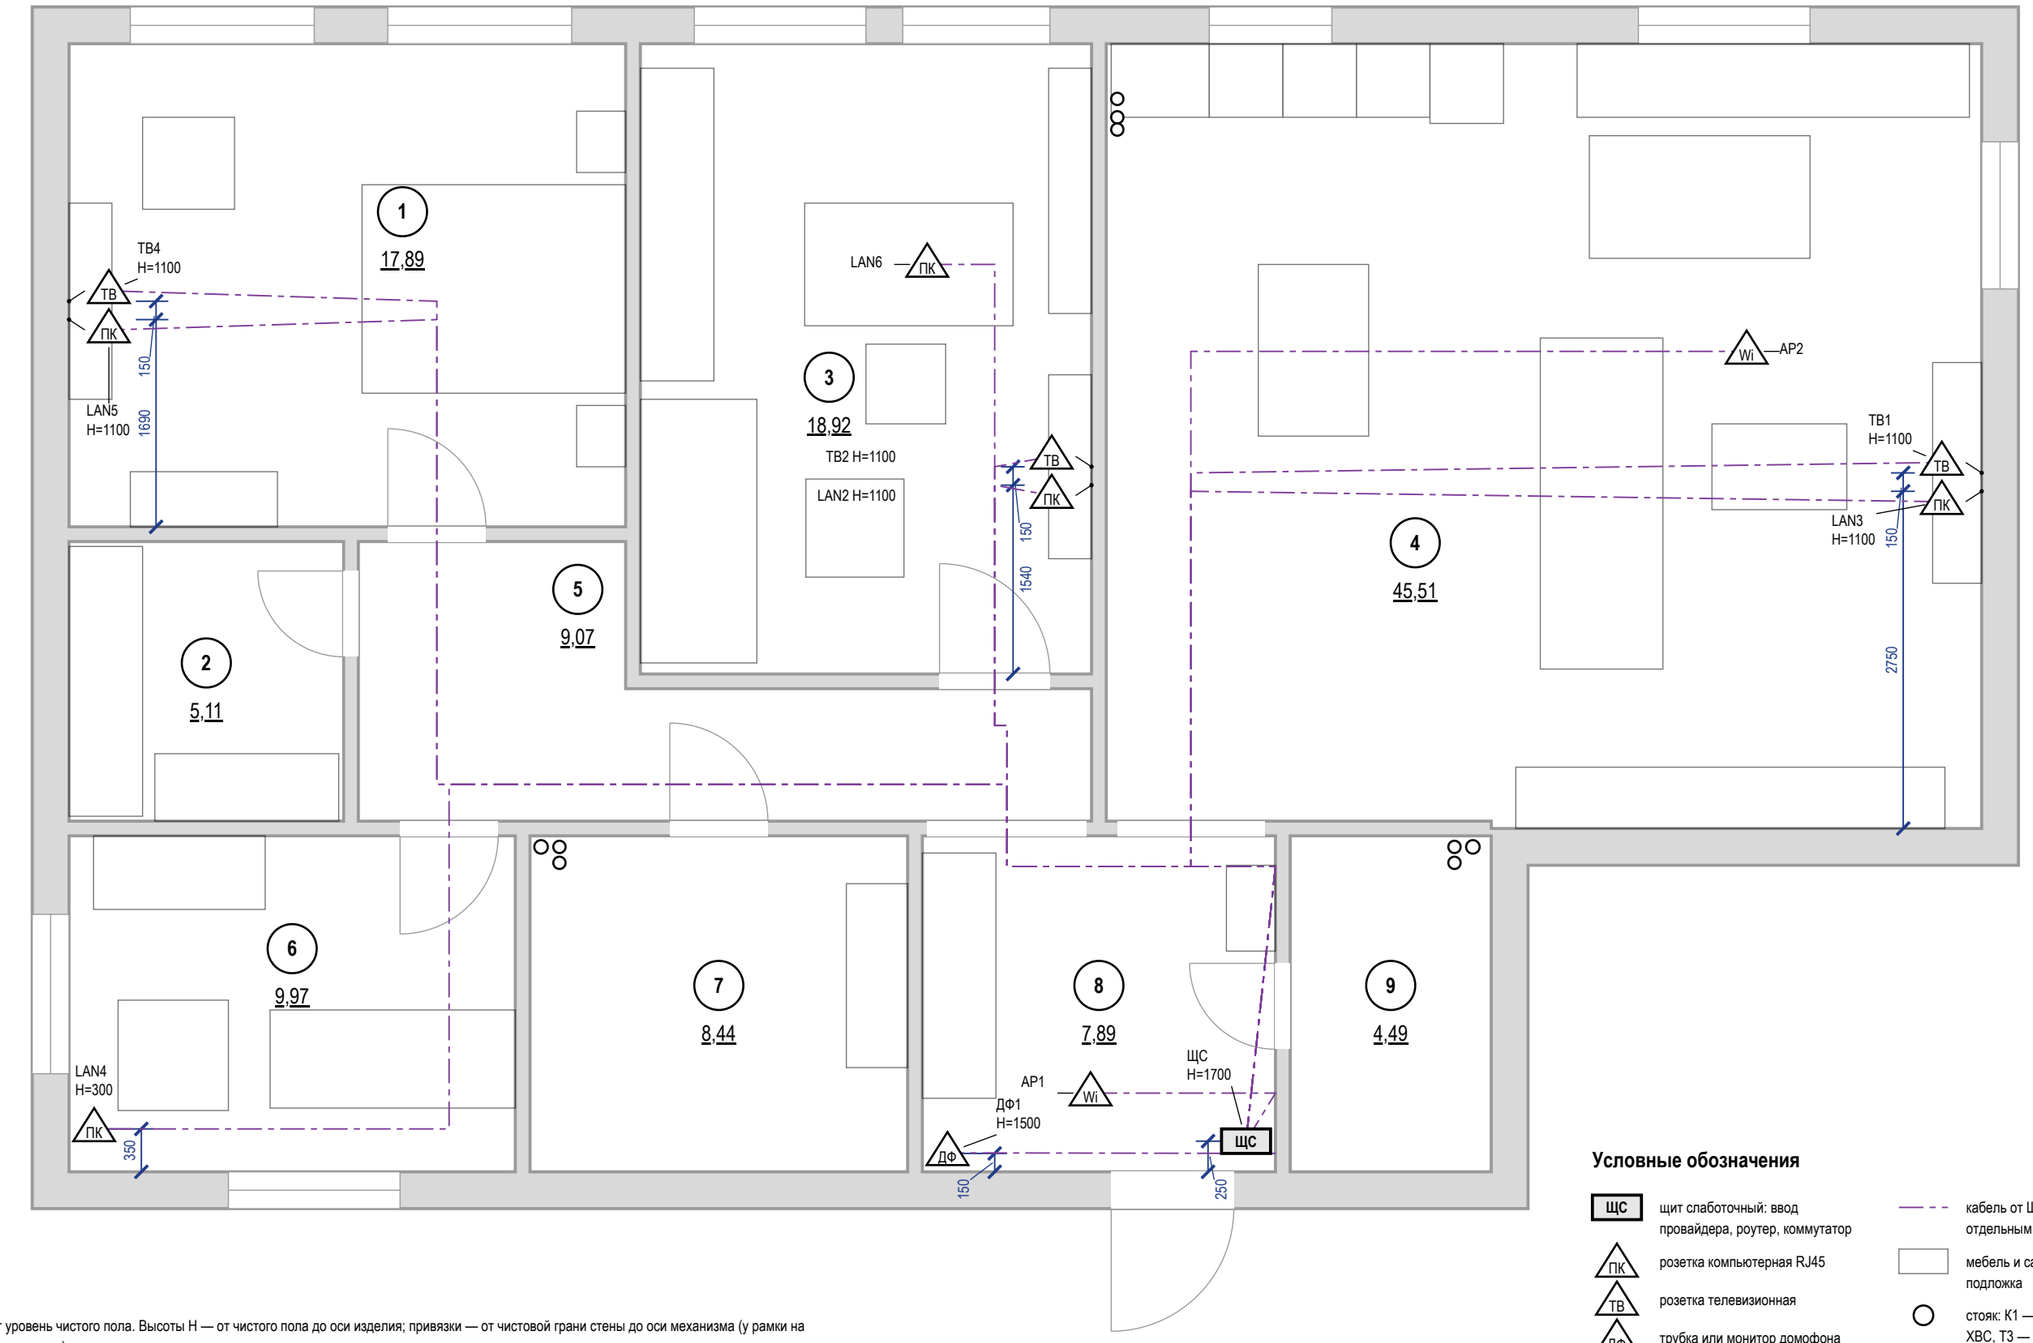


Примечания

1. За отметку 0,000 принят уровень чистого пола. Высоты Н — от чистого пола до оси изделия; привязки — от чистовой грани стены до оси механизма (у рамки на несколько постов — до оси рамки).
2. Высота установки, не указанная на плане: розетки LAN и ТВ — 300 мм от чистого пола.
3. Слаботочные кабели — отдельно от силовых: в своей трубе или лотке, при параллельной прокладке не ближе 100 мм к силовым, пересечения под прямым углом; каждую точку — отдельным кабелем от ЩС без скруток.
4. Трассы на листе — принципиальные; фактические зафиксировать исполнительной схемой до закрытия отделкой. Силовые линии, УЗО 30 мА, ДСУП, кабель нг(А)-LS — по листам розеток и щита.
5. Проект силовой части и расчёт токов КЗ — по проекту ЭОМ; слаботочная часть согласуется с провайдером и управляющей компанией (домофон, коллективное ТВ).

Условные обозначения

- ЩС — щит слаботочный: ввод провайдера, роутер, коммутатор
- ПК — розетка компьютерная RJ45
- ТВ — розетка телевизионная
- ДФ — трубка или монитор домофона
- Wi — точка доступа Wi-Fi (питание PoE)
- кабель от ЩС до точки, отдельным лучом
- мебель и сантехприборы подложка
- стояк: К1 — канализация, В1 ХВС, Т3 — ГВС
- 1 — номер помещения, площадь м²

					Проект: Квартира с кабинетом — М 1:50
	Лист	№ док.	Подпись	Дата	План слаботочных сетей
Дизайнер	Кырлан А.С.			04.11.26	Стадия: П; Лист: 66; Листов: 127

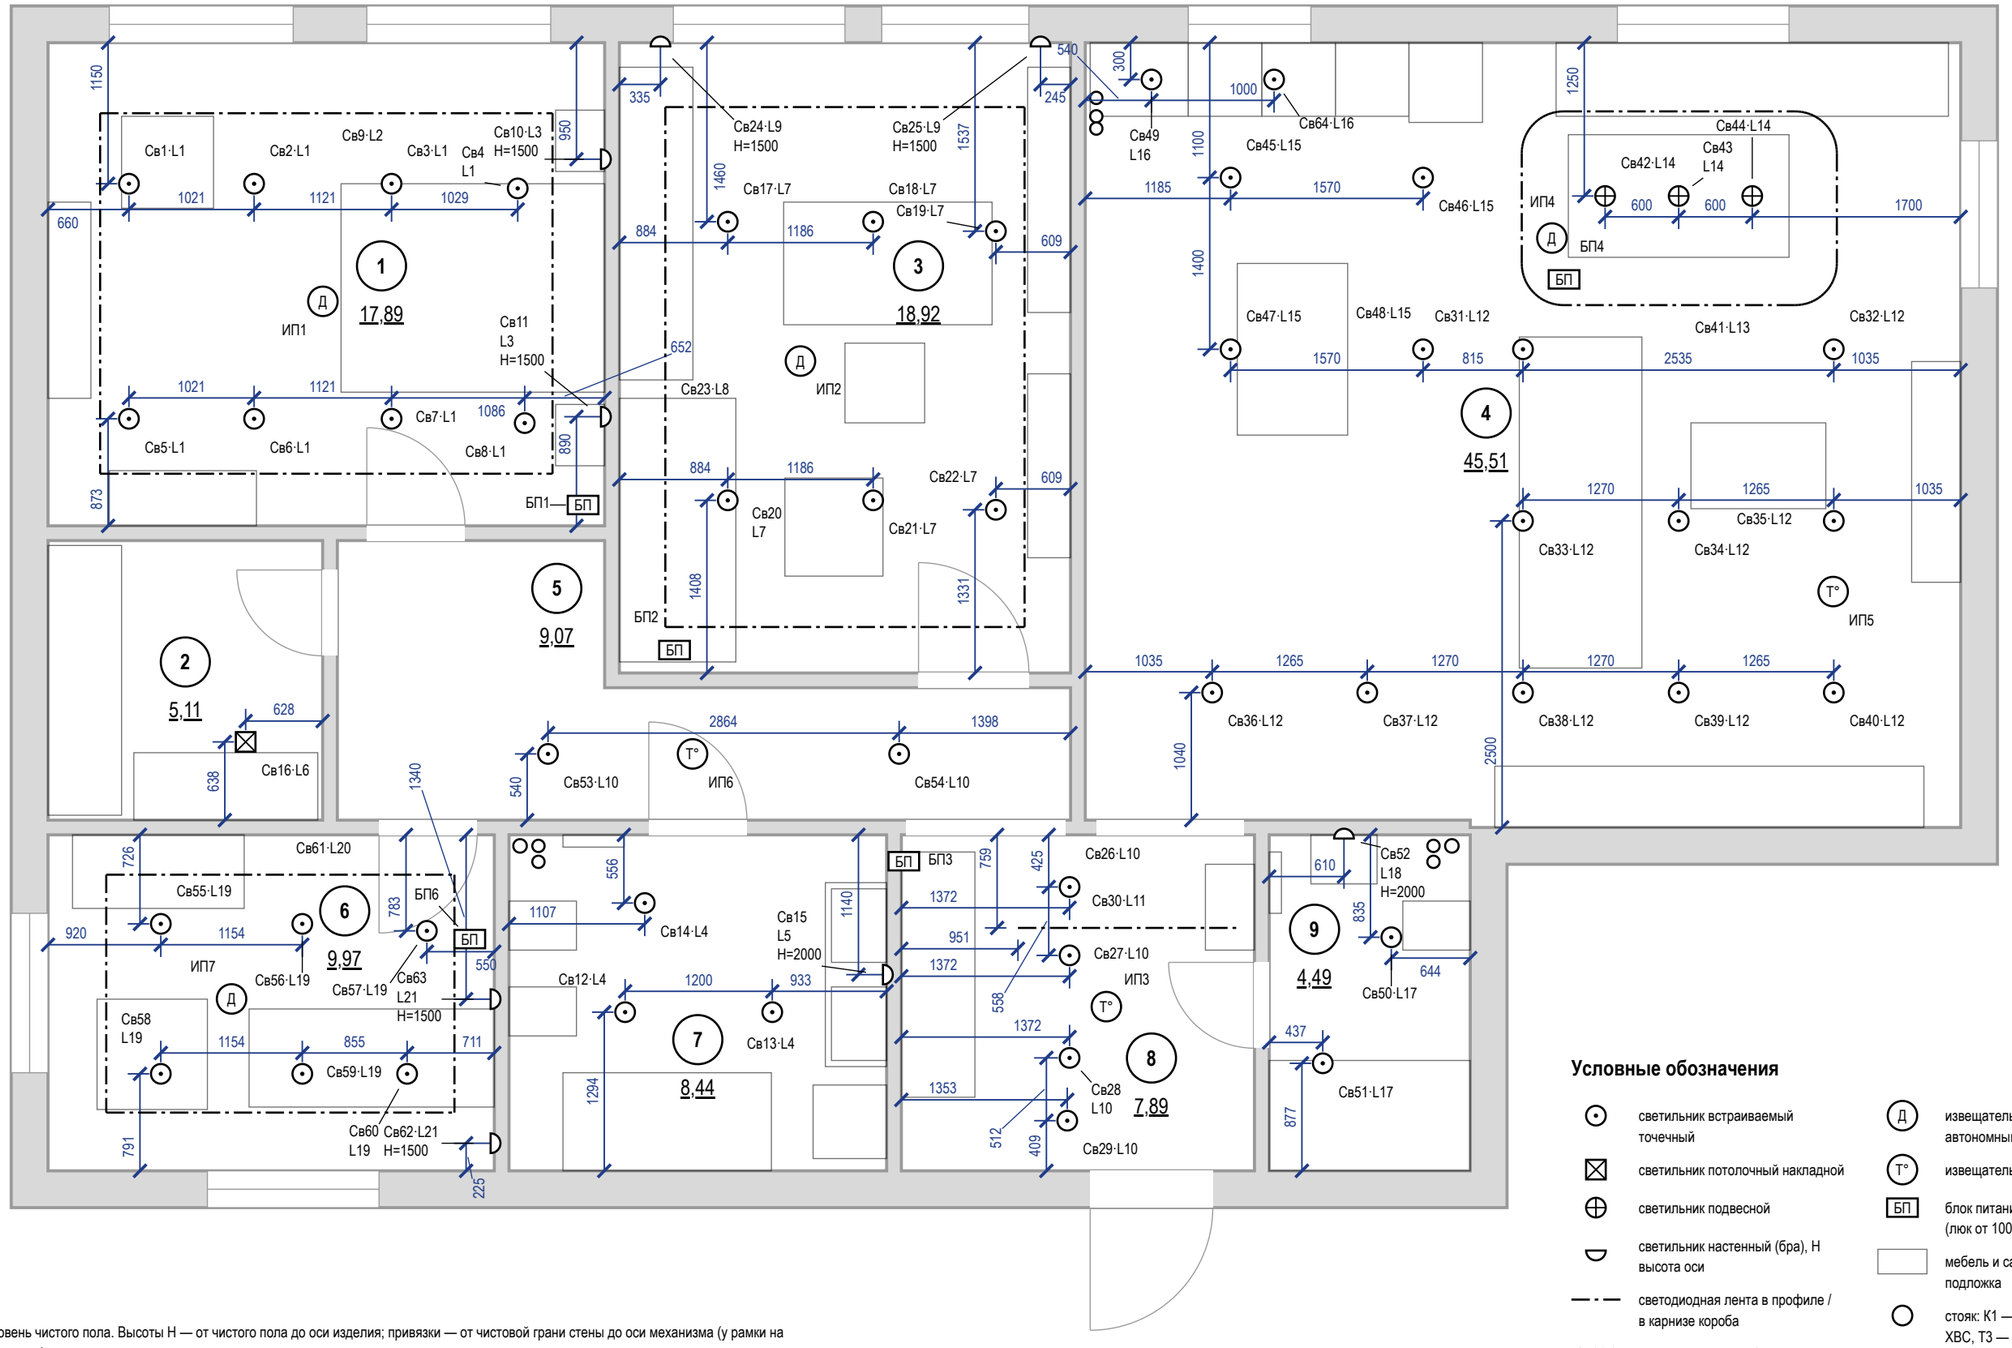

Примечания

1. За отметку 0,000 принят уровень чистого пола. Высоты H — от чистого пола до оси изделия; привязки — от чистовой грани стены до оси механизма (у рамки на несколько постов — до оси рамки).
2. Высота установки, не указанная на плане: светильники — на потолке; настенные — по отметке H у знака. Привязки — до оси светильника от чистовой грани стены, по рядам.
3. Во влажных помещениях — светильники не ниже IP44; в зонах 0–2 ванной — по ГОСТ Р 50571.7.701-2024 (зона 1 — IPX5).
4. LED-лента в карнизе подсветки короба — по линии карниза с плана потолков; блок питания — в люке короба (БП на плане), питание ленты длиннее 5 м — с двух концов.
5. Розеточные и мокрые линии — через УЗО или дифавтомат с током утечки не более 30 мА (ПУЭ 7.1.79); в санузле выполнить ДСУП (ПУЭ 7.1.87–7.1.88).
6. Кабель — медный, исполнение нг(A)-LS (ГОСТ 31565-2012); скрытая прокладка только горизонтально и вертикально, фактические трассы зафиксировать исполнительной схемой до закрытия отделкой.
7. Расчёт нагрузок, токов КЗ, селективности и сечений — по проекту ЭОМ организации с допуском СРО; лист задаёт состав, расположение и группы.
8. Ведомость светильников (тип, количество, мощность, поток, Tц, Ra) — лист 68.

Условные обозначения

- светильник встраиваемый точечный
- светильник потолочный накладной
- светильник подвесной
- светильник настенный (бра), H высота оси
- светодиодная лента в профиле / в карнизе короба
- Св1·L1 — марка светильника (как в ведомости и на развёртках) · группа включения L (лист 69)
- Д — извещатель пожарный дымовой автономный
- T° — извещатель пожарный тепловой
- БП — блок питания LED, с доступом (люк от 100×100 мм)
- мебель и сантехприборы подложка
- стояк: К1 — канализация, В1 ХВС, Т3 — ГВС
- 1 — номер помещения, площадь м²

					Проект: Квартира с кабинетом — М 1:50
	Лист	№ док.	Подпись	Дата	
Дизайнер	Кырлан А.С.			04.11.26	План освещения

Стадия	Лист	Листов
П	67	127

выпуск 04.11.2026 № 627e1ac6ce · стр. 67 из 127

Параметры светильников для подбора

Поз.	Марки	Наименование	Установка	Кол.	P, Вт	Σ P, Вт	Ф, лм	Тц, К	Ra	Угол, °	IP	Дим.	Слой	Группа	Пом.
1	Св1–Св8	Встраиваемый точечный	в ГКЛ, корпус ≤ 70 мм	8	12	96	1000	2700	90	—	20	—	общий	L1	1
2	Св9	Лента светодиодная 24 В	в карнизе короба, профиль с рассеивателем	13,3 м	9,6/м	127,3	900/м	2700	90	—	20	да	акцентный	L2	1
3	Св10, Св11, Св24, Св25, Св62, Св63	Настенный (бра)	на стене, H=1500	6	6	36	400	2700	90	60	20	—	рабочий	L3, L9, L21	1, 3, 6
4	Св16	Потолочный накладной	на потолке, засветка стены	1	10	10	900	3000	90	—	20	—	общий	L6	2
5	Св17–Св22, Св55–Св60	Встраиваемый точечный	в ГКЛ, корпус ≤ 70 мм	12	12	144	1050	2700	90	—	20	—	общий	L7, L19	3, 6
6	Св23	Лента светодиодная 24 В	в карнизе короба, профиль с рассеивателем	14,3 м	9,6/м	137,7	900/м	2700	90	—	20	да	акцентный	L8	3
7	Св31, Св32, Св33, Св34, Св35, Св36, Св37, Св38, Св39, Св40	Встраиваемый точечный	в ГКЛ, корпус ≤ 70 мм	10	12	120	1000	3000	90	—	20	да	общий	L12	4
8	Св41	Лента светодиодная 24 В	в нише уровня, профиль с рассеивателем	7,7 м	9,6/м	74,1	900/м	2700	90	—	20	да	акцентный	L13	4
9	Св42, Св43, Св44	Подвесной	подвес, низ H=1450	3	9	27	800	3000	90	—	20	да	общий	L14	4
10	Св45, Св46, Св47, Св48	Встраиваемый точечный	в ГКЛ, корпус ≤ 70 мм	4	10	40	900	3000	90	—	20	—	общий	L15	4
11	Св26–Св29, Св49, Св53, Св54, Св64	Встраиваемый точечный	в ГКЛ, корпус ≤ 70 мм	8	7	56	600	3000	90	—	20	да	общий, рабочий	L10, L16	4, 5, 8
12	Св61	Лента светодиодная 24 В	в карнизе короба, профиль с рассеивателем	9,6 м	9,6/м	91,8	900/м	2700	90	—	20	да	акцентный	L20	6
13	Св12–Св14, Св51	Встраиваемый точечный	в ГКЛ, корпус ≤ 70 мм	4	6	24	500	3000	90	—	44	—	общий	L4, L17	7, 9
14	Св15, Св52	Настенный светильник над зеркалом, драйвер встроен	над зеркалом, H=2000	2	8	16	600	3000	90	—	44	—	рабочий	L5, L18	7, 9
15	Св30	Лента светодиодная 24 В	на поверхности, профиль с рассеивателем, датчик движения	1,8 м	4,8/м	8,6	150/м	2700	90	—	20	нет	ночной	L11	8
16	Св50	Встраиваемый точечный	в ГКЛ, корпус ≤ 70 мм	1	7	7	600	3000	90	—	44	—	общий	L17	9
		Итого		**59 шт + 46,7 м**		**1015,5**									

LED-ленты, линейные светильники и блоки питания

Марка	Пом.	L, м	U, В	Вт/м	Σ P, Вт	БП	P БП, Вт	Загр., %	Питание	Доступ к БП
Св9	1	13,3	24	9,6	127,3	БП1	200	64	с двух концов	люк 300×300 в коробе потолка ПТ1
Св23	3	14,3	24	9,6	137,7	БП2	200	69	с двух концов	люк 300×300 в коробе потолка ПТ1
Св41	4	7,7	24	9,6	74,1	БП4	300	25	с двух концов	люк 300×300 в нише фигуры потолка ПТ1
Св61	6	9,6	24	9,6	91,8	БП6	200	46	с двух концов	люк 300×300 в коробе потолка ПТ1
Св30	8	1,8	24	4,8	8,6	БП3	20	43	с одного конца	в шкафу M_30, верхняя полка


Сценарии (помещения со светорегуляторами)

Помещение	Сценарий	Горят группы (уровень)	Управление
4. Кухня-гостиная	Вечер	L12 споты гостиной — 30 %; L13 подсветка короба — 100 %; L14 подвесы над столом — 50 %; остальные выкл.	светорегуляторы S8, S9, S17
	Ужин	L13 подсветка короба — 60 %; L14 подвесы над столом — 100 %; L16 подсветка столешницы — 30 %; остальные выкл.	светорегуляторы S9, S10, S17
	Кино	L13 подсветка короба — 20 %; остальные выкл.	светорегулятор S17
	Готовка	L12 споты гостиной — 50 %; L15 споты кухни — вкл.; L16 подсветка столешницы — 100 %; остальные выкл.	светорегуляторы S8, S10; выключатель S18

Примечания

1. Позиции и марки Св — те же, что на плане освещения (лист 67); группы L — по плану выключателей (лист 69).
2. Модели светильников не выбраны: лист — техническое задание на подбор. Модель по строке таблицы: поток, Тц, Ra, угол, IP и регулировка яркости не хуже указанных, мощность не больше; встраиваемые — под глубину короба (графа «Установка»). IP 20 — сухие помещения. После выбора моделей (артикул, производитель) лист выпускается как «Спецификация светильников».
3. Длина LED-ленты в карнизе и нише уровня — по линиям карниза и ниши плана потолков (лист 57); Σ P = Вт/м × длина. Блок питания загружен не больше чем на 80 %; лента 24 В длиннее 10 м питается с двух концов; доступ к блоку питания — люк ревизии 300×300 мм или место, указанное в таблице.
4. Сценарии: % — яркость группы на светорегуляторе; «вкл.» — группа на обычной клавише; группы, не названные в строке, выключены. Светильники и блоки питания групп на светорегуляторе — с регулировкой яркости. Клавиши и светорегуляторы — лист 69.
5. В пом. 1, 3, 6 свет включается клавишами групп — лист 69.
6. Мощность и поток в таблице — требования к подбору (поток не меньше, мощность не больше указанных); после выбора модели — по её паспорту, Σ P — установленная мощность освещения. Оценка освещённости — на плане освещения; это не светотехнический расчёт.

					Проект: Квартира с кабинетом
	Лист	№ док.	Подпись	Дата	
Дизайнер	Кырлан А.С.			04.11.26	Техническое задание на подбор светильников
					Стадия: П; Лист: 68; Листов: 127

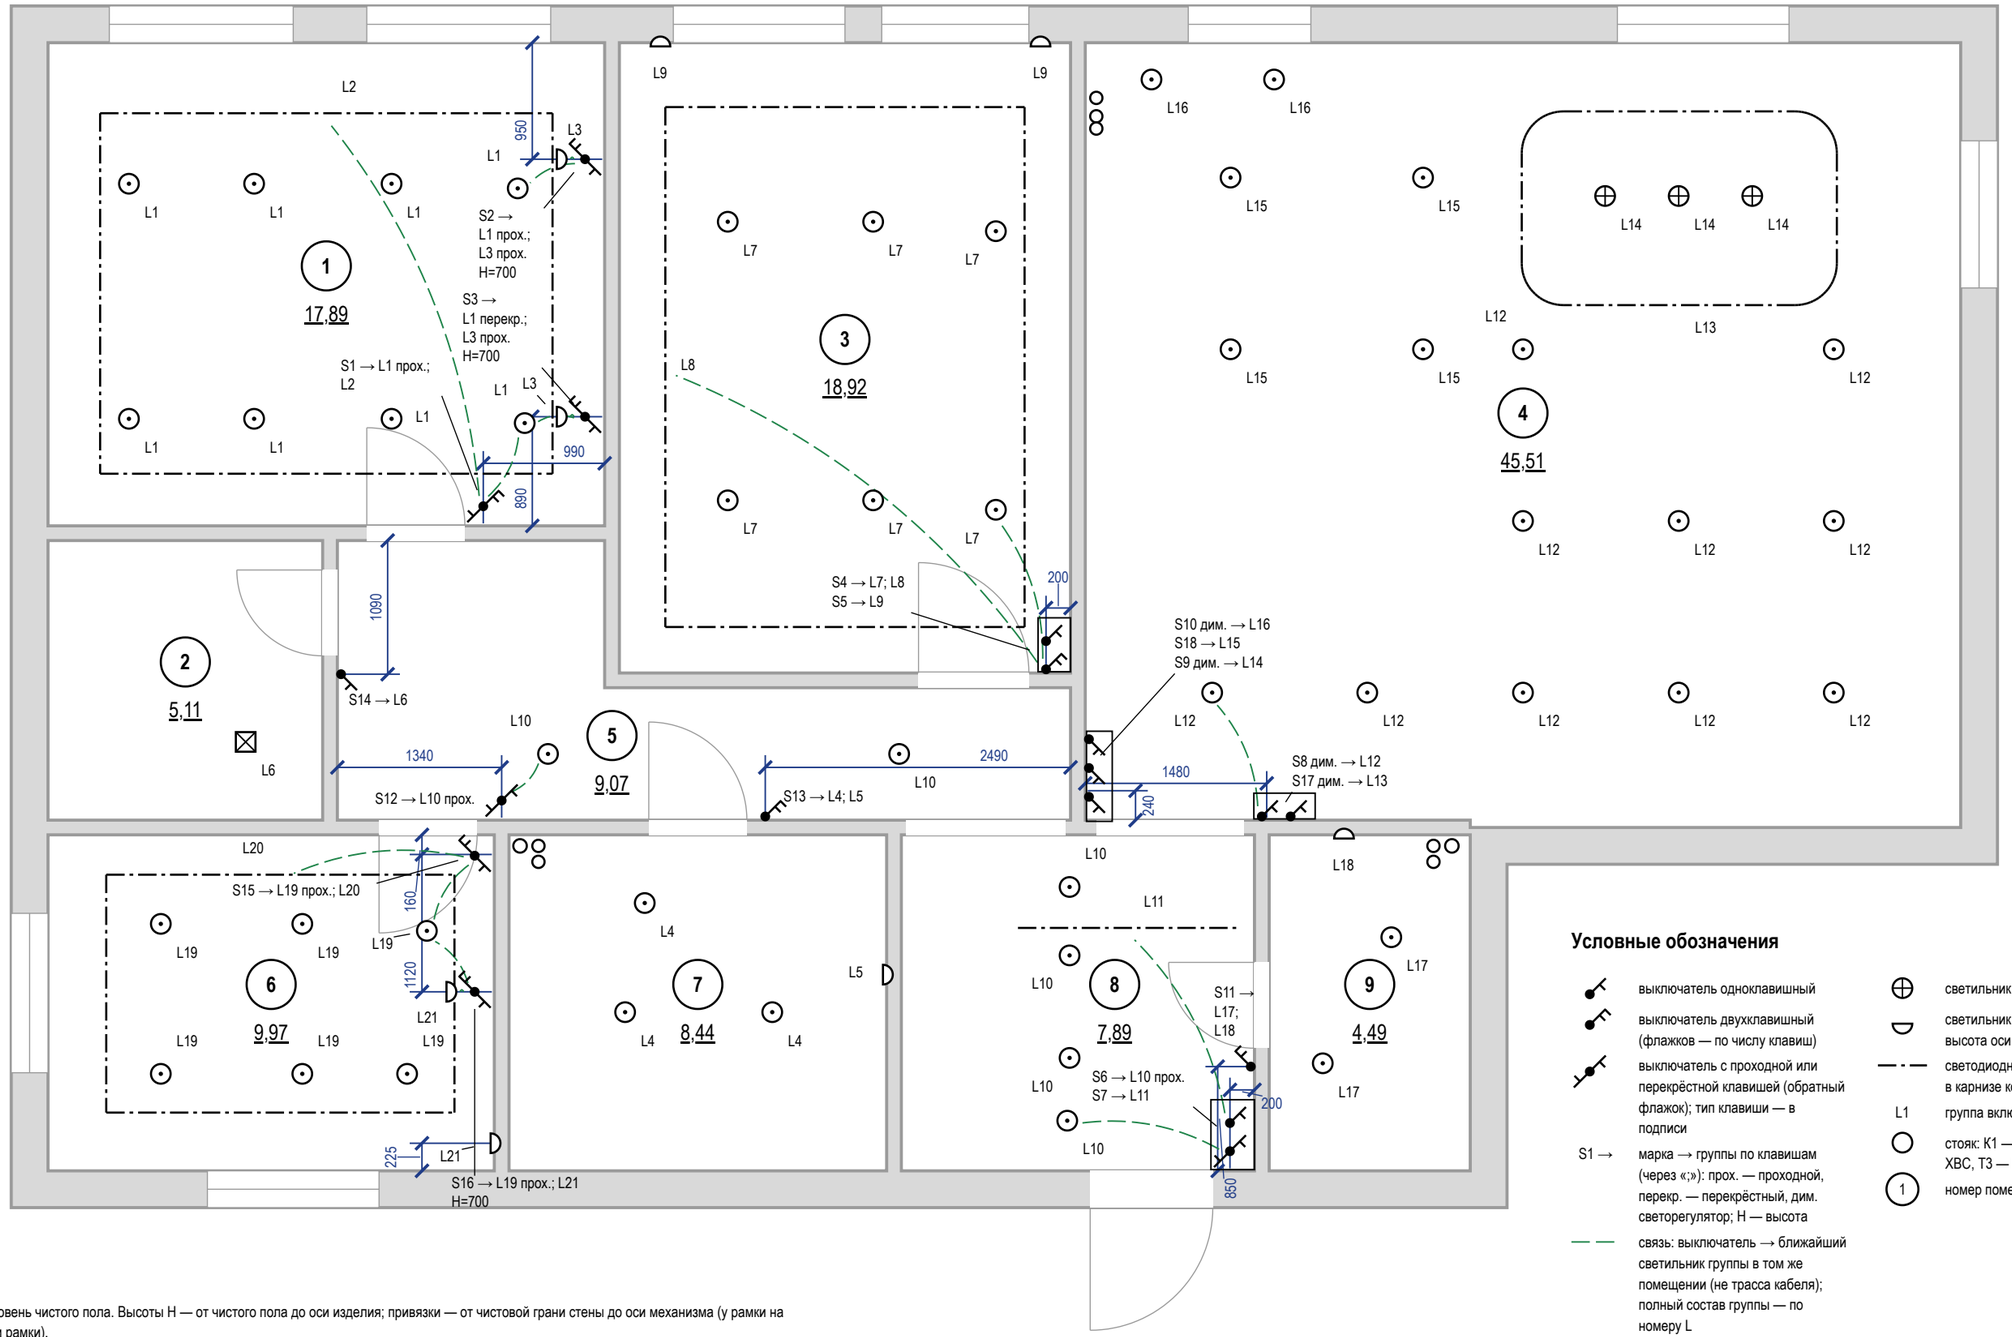


Условные обозначения

- выключатель одноклавишный
- выключатель двухклавишный (флажков — по числу клавиш)
- выключатель с проходной или перекрёстной клавишей (обратный флажок); тип клавиши — в подписи
- S1 → — марка → группы по клавишам (через «;»): прох. — проходной, перекр. — перекрёстный, дим. светорегулятор; H — высота
- связь: выключатель → ближайший светильник группы в том же помещении (не трасса кабеля); полный состав группы — по номеру L
- светильник встраиваемый точечный
- светильник потолочный накладной
- светильник подвесной
- светильник настенный (бра), H высота оси
- светодиодная лента в профиле / в карнизе короба
- L1 — группа включения у светильника
- стояк: К1 — канализация, В1 ХВС, Т3 — ГВС
- 1 — номер помещения, площадь м²

Примечания

1. За отметку 0,000 принят уровень чистого пола. Высоты H — от чистого пола до оси изделия; привязки — от чистовой грани стены до оси механизма (у рамки на несколько постов — до оси рамки).
2. Высота установки, не указанная на плане: выключатели — 900 мм от чистого пола (у кровати и другие — H у марки), со стороны дверной ручки (ПУЭ 7.1.51).
3. Какой выключатель какие светильники включает — по номеру группы L: у выключателя (S1 → L1; L2 — клавиши по порядку) и у каждого светильника. Пунктир подсказка к ближайшему светильнику группы в том же помещении (не дальше 3 м), это не трасса кабеля; выключатель за стеной (у двери санузла) и далёкая группа — только номер группы.
4. Группы из нескольких мест (L1 — S1, S2, S3; L3 — S2, S3; L10 — S6, S12; L19 — S15, S16): на крайних местах — проходные клавиши, на промежуточных перекрёстные; механизмы — в ведомости изделий.
5. Светорегулятор — по заднему фронту (для LED-драйверов), совместимость с драйверами проверить до закупки.
6. Розеточные и мокрые линии — через УЗО или дифавтомат с током утечки не более 30 мА (ПУЭ 7.1.79); в санузле выполнить ДСУП (ПУЭ 7.1.87–7.1.88).
7. Кабель — медный, исполнение нг(A)-LS (ГОСТ 31565-2012); скрытая прокладка только горизонтально и вертикально, фактические трассы зафиксировать исполнительной схемой до закрытия отделкой.
8. Расчёт нагрузок, токов КЗ, селективности и сечений — по проекту ЭОМ организации с допуском СРО; лист задаёт состав, расположение и группы.

					Проект: Квартира с кабинетом	М 1:50
	Лист	№ док.	Подпись	Дата		
Дизайнер	Кырлан А.С.			04.11.26	Управление светильниками	Стадия: П; Лист: 69; Листов: 127

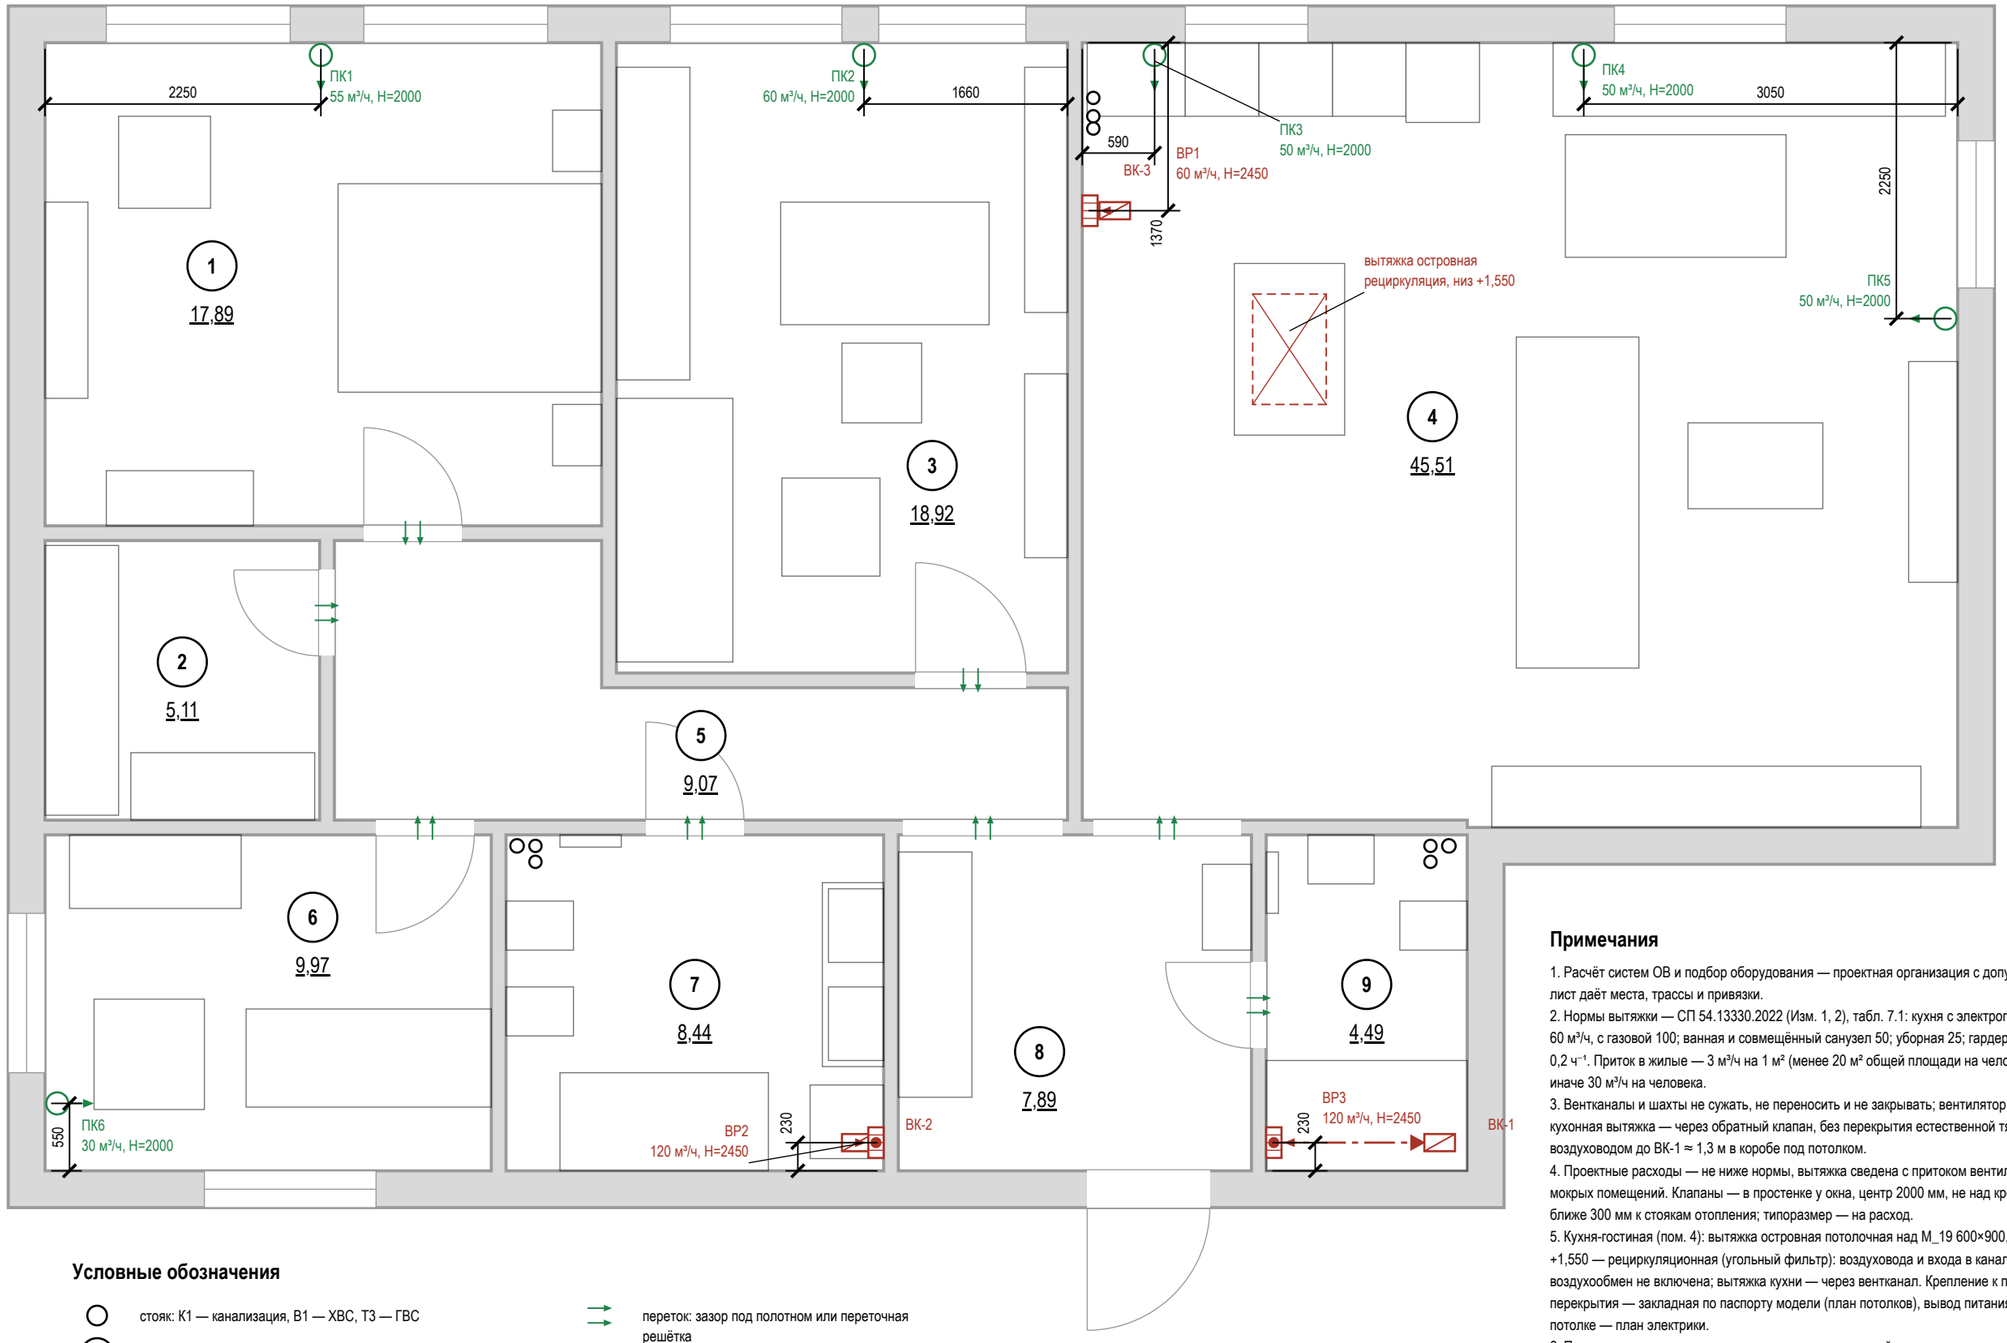

Условные обозначения


- стояк: К1 — канализация, В1 — ХВС, Т3 — ГВС
- (1) номер помещения, площадь м²
- вытяжная решётка в вентканал: марка, расход м³/ч, Н центра от чистого пола
- вытяжная решётка с бытовым вентилятором и обратным клапаном: марка, расход, Н
- приточный клапан (КИВ) в наружной стене: марка, расход, Н центра
- переток: зазор под полотном или переточная решётка
- кухонная вытяжка над варочной панелью
- вентканал ВК-N в стене или вентблоке
- воздуховод в коробе под потолком (за подшивным потолком) до вентканала
- отдельный вход воздуховода в вентканал, обратный клапан

Примечания

1. Расчёт систем ОВ и подбор оборудования — проектная организация с допуском СРО; лист даёт места, трассы и привязки.
2. Нормы вытяжки — СП 54.13330.2022 (Изм. 1, 2), табл. 7.1: кухня с электроплитой 60 м³/ч, с газовой 100; ванная и совмещённый санузел 50; уборная 25; гардеробная 0,2 ч⁻¹. Приток в жилые — 3 м³/ч на 1 м² (менее 20 м² общей площади на человека), иначе 30 м³/ч на человека.
3. Вентканалы и шахты не сужать, не переносить и не закрывать; вентилятор и кухонная вытяжка — через обратный клапан, без перекрытия естественной тяги; ВР3 воздуховодом до ВК-1 ≈ 1,3 м в коробе под потолком.
4. Проектные расходы — не ниже нормы, вытяжка сведена с притоком вентиляторами мокрых помещений. Клапаны — в простенке у окна, центр 2000 мм, не над кроватью, не ближе 300 мм к стоякам отопления; типоразмер — на расход.
5. Кухня-гостиная (пом. 4): вытяжка островная потолочная над М_19 600×900, низ +1,550 — рециркуляционная (угольный фильтр): воздуховода и входа в канал нет, в воздухообмен не включена; вытяжка кухни — через вентканал. Крепление к плите перекрытия — закладная по паспорту модели (план потолков), вывод питания на потолке — план электрики.
6. Переток — зазор под полотнами межкомнатных дверей или переточная решётка.
7. Кондиционирование заданием не предусмотрено; при установке трассы фреона и дренажа (не менее 40 мм/м, в К1 через сифон) и питание заложить до черновых работ.
8. Привязки оборудования — по паспортам приобретённых моделей, до черновых работ.

					Проект: Квартира с кабинетом	М 1:50
	Лист	№ док.	Подпись	Дата	План вентиляции	Стадия / Лист / Листов
Дизайнер	Кырлан А.С.			04.11.26		П / 70 / 127

выпуск 04.11.2026 № 627e1ac6ce · стр. 70 из 127

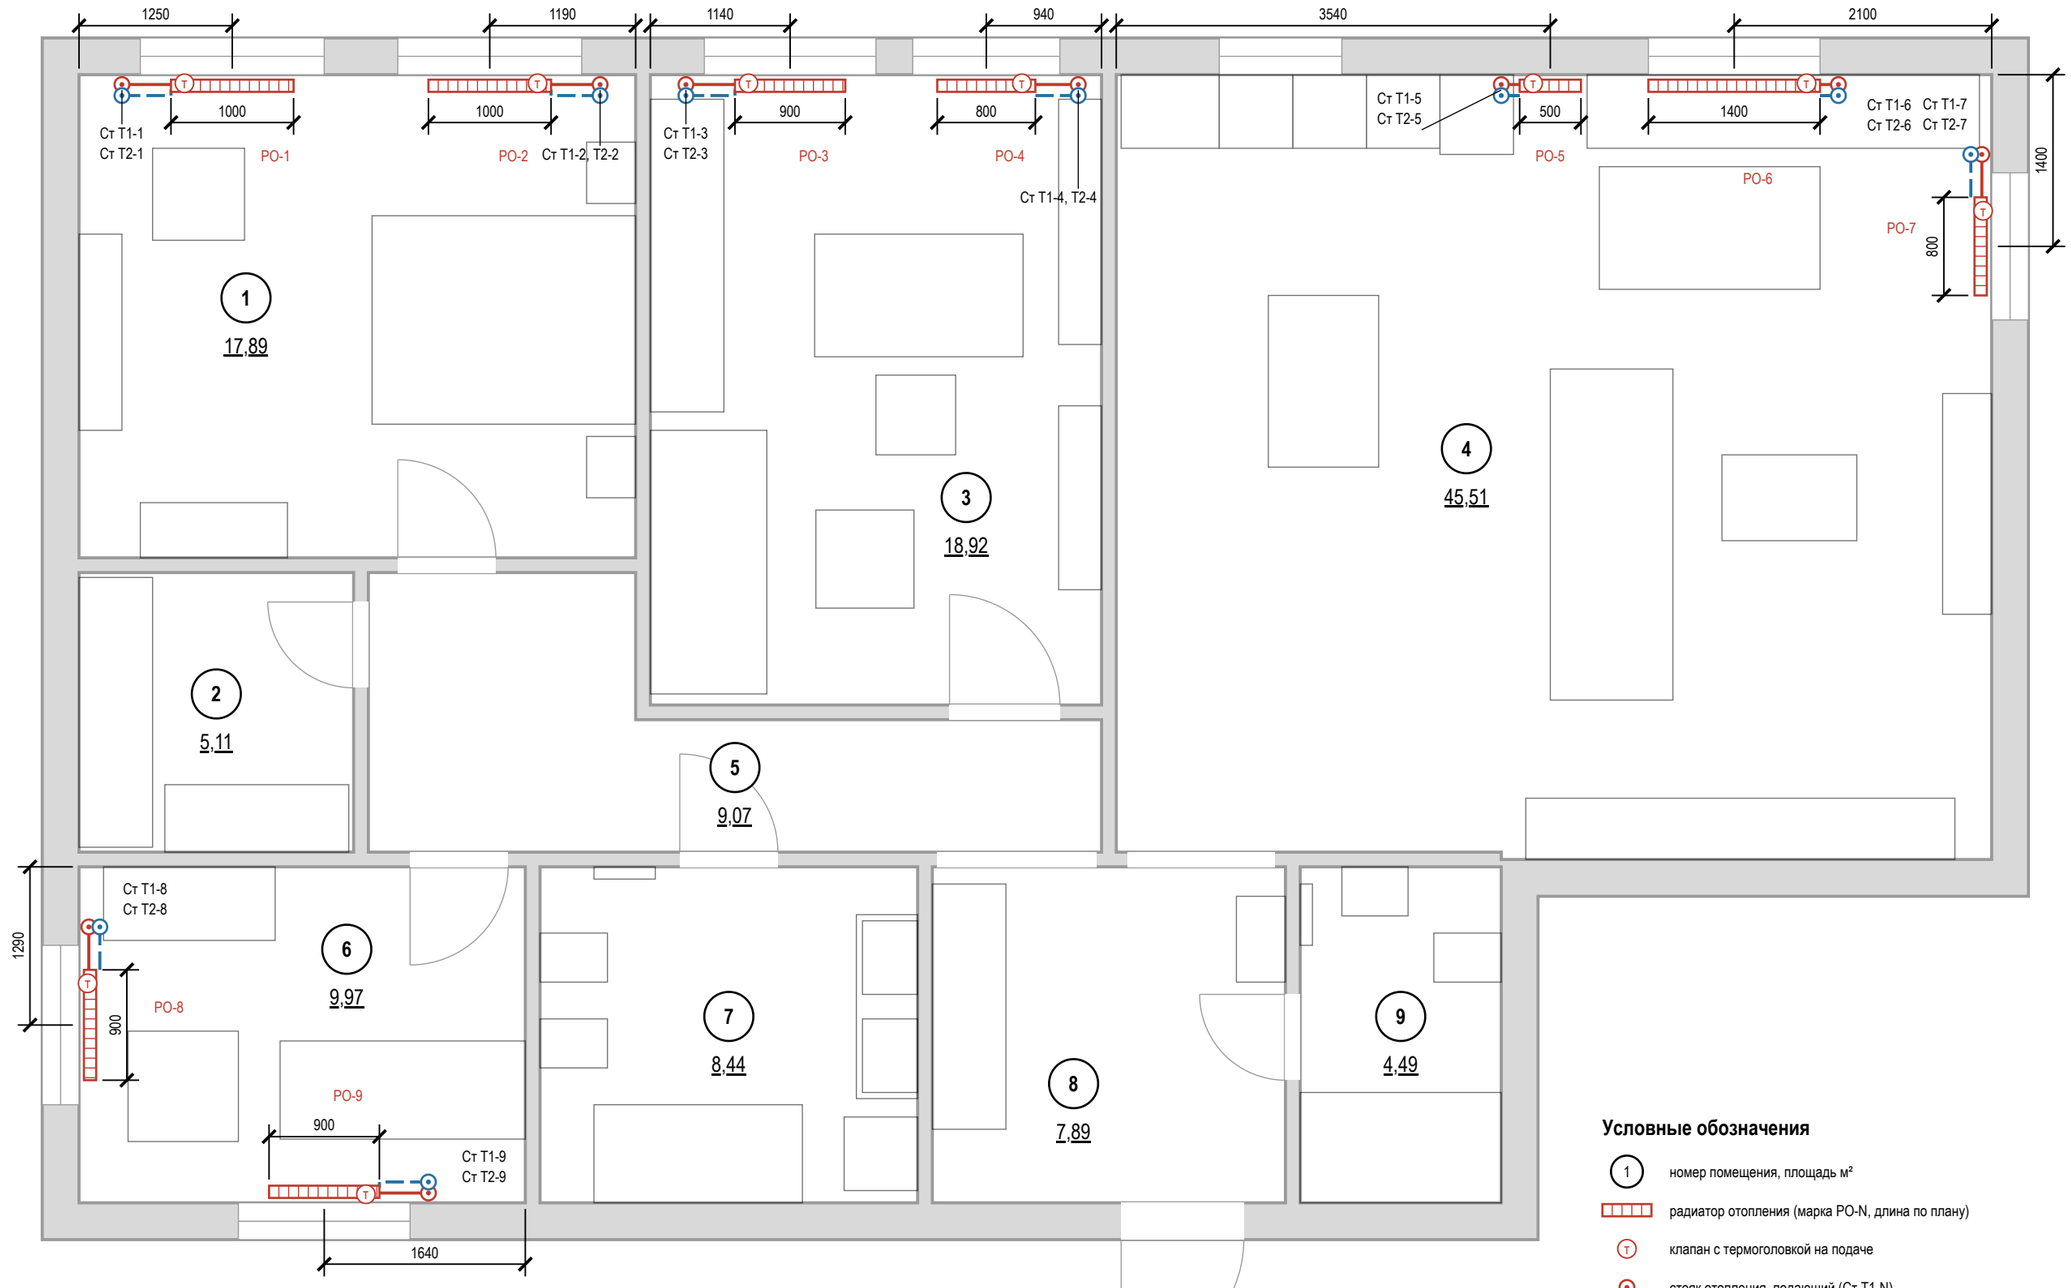

Условные обозначения

- (1) — номер помещения, площадь м²
- радиатор отопления (марка PO-N, длина по плану)
- (T) — клапан с термоголовкой на подаче
- стояк отопления, подающий (Ст T1-N)
- стояк отопления, обратный (Ст T2-N)
- T1 — отопление, подающий трубопровод
- T2 — отопление, обратный трубопровод

Примечания


1. Расчёт системы отопления, теплопотерь и подбор приборов — проектная организация с допуском СРО; лист даёт места и привязки.
2. Тип, длина и мощность радиаторов — по теплотехническому расчёту; лист задаёт места, зазоры и подключение.
3. Зазоры радиатора: низ не менее 100 мм от чистого пола, верх не менее 100 мм до подоконника, 30–50 мм от стены до задней панели; центр по оси окна с допуском ±20 мм. Верх до подоконника — 180 мм (PO-6 — 580).
4. Радиаторы не закрывать глухими коробами и мебелью; перенос и замена приборов в многоквартирном доме — переустройство, согласование с управляющей организацией (ЖК РФ ст. 25–26); вынос на лоджию запрещён.
5. Исключение — экран-мебель с решёткой: M_20 (пом. 4), щель 60 мм у стены, решётка в лицевой панели, зазор до прибора 50 мм: теплоотдача прибора за экраном снижается — мощность с учётом экрана по теплотехническому расчёту; сиденье над прибором — съёмное для доступа к крану.
6. Трубы отопления через межквартирные стены не прокладывать (СП 51.13330.2011, п. 9.19); через перекрытия и перегородки — в гильзах.
7. Привязки приборов и подводок — по паспортам приобретённых радиаторов и клапанов, до черновых работ.
8. Привязки — до обмера: Стояки отопления в исходных данных не заданы: показаны у откосов окон и у торцов приборов, подводки — принципиально. До черновых работ — обмер стояков и паспорта приборов; лист перевыпустить по факту.
9. До закрытия отделкой трубопроводы отопления испытать гидростатическим давлением с оформлением акта (СП 73.13330.2016, 7.2–7.3).

					Проект: Квартира с кабинетом — М 1:50
	Лист	№ док.	Подпись	Дата	План отопления
Дизайнер	Кырлан А.С.			04.11.26	Стадия: П; Лист: 71; Листов: 127




выпуск 04.11.2026 № 627e1ac6ce · стр. 71 из 127

Отметки по высоте

±0,000 чистый пол пом. 1–6, 8; отсчёт высот
−0,015 чистый пол пом. 7, 9, ниже на 15 мм
−0,064 верх плиты — расчёт, не замер (задание на обмер)
сущ. пол снимается до плиты; не замерен (задание на обмер)

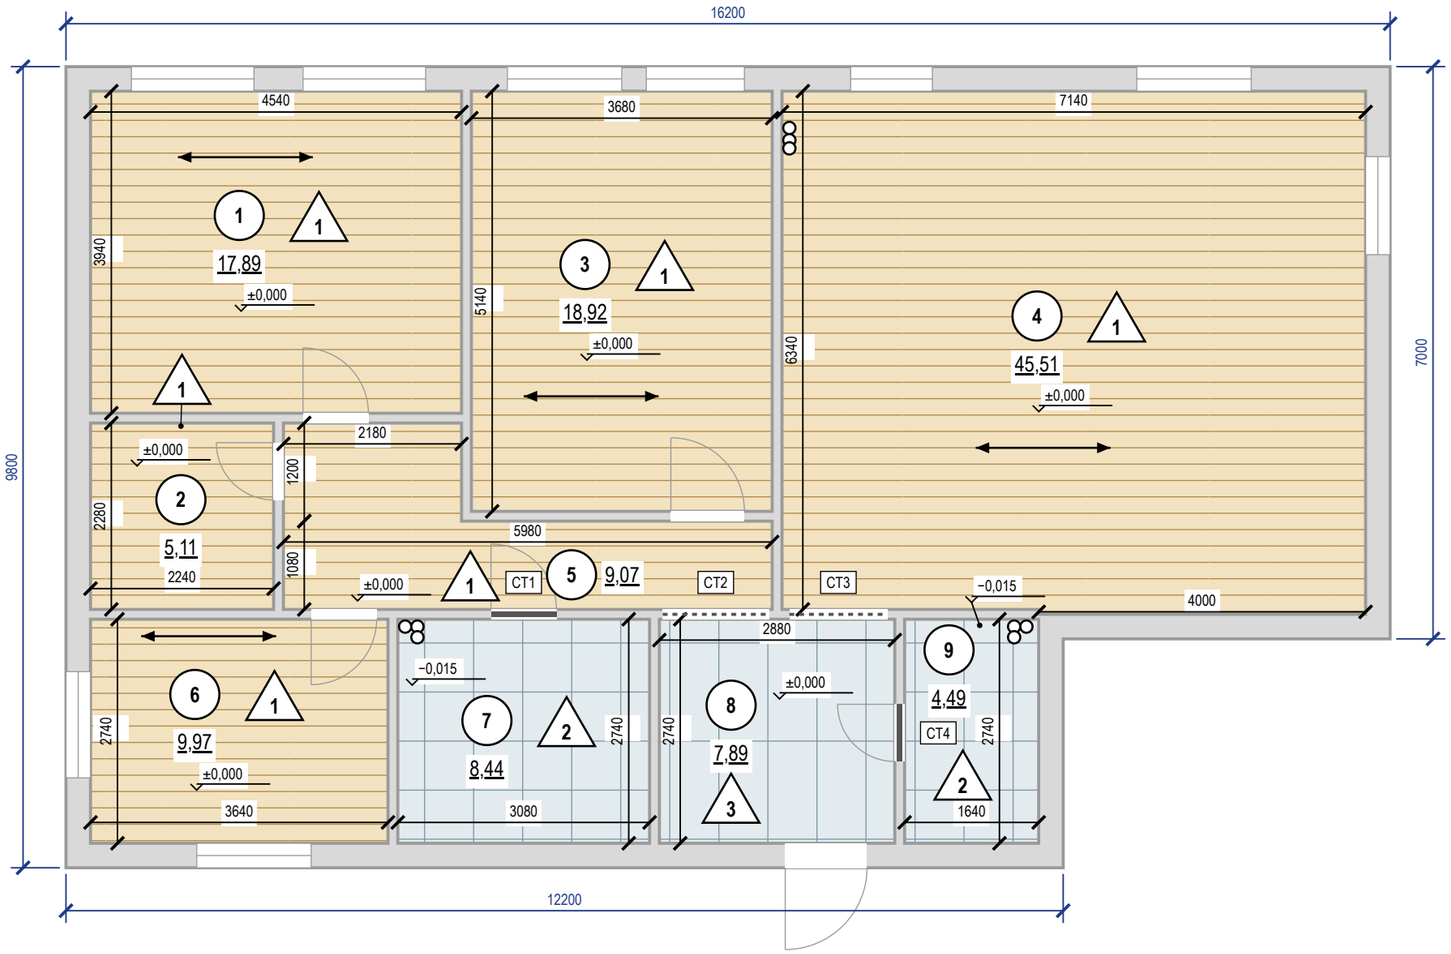

Экспликация полов

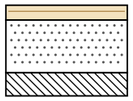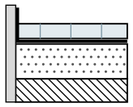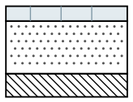Номер помещения	Тип пола	Схема пола	Данные элементов пола (наименование, толщина, основание), мм	Площадь, м²
1, 2, 3, 4, 5, 6	1		Инженерная доска на клею — 14 Стяжка ЦПС М200 — 50 Плита перекрытия Всего 64 мм; ЧП ±0,000, верх плиты −0,064	106,47
7, 9	2		Керамогранит на клею C2 TE S1 — 14 Гидроизоляция обмазочная, 2 слоя, с заведением на стены 200 мм — 2 Стяжка ЦПС М200 — 33 Плита перекрытия Всего 49 мм; ЧП −0,015, верх плиты −0,064	12,93
8	3		Керамогранит на клею C2 TE S1 — 14 Стяжка ЦПС М200 — 50 Плита перекрытия Всего 64 мм; ЧП ±0,000, верх плиты −0,064	7,89
			Итого	**127,29**

Раскладка покрытий

Пом.	Укладка	Старт (оси от чистовых стен), мм	Отступ 1-го ряда / крайние плитки, мм
1	вдоль стен А/В, прямая	от стены А, 1-й ряд вдоль неё	зазор от стены не задан
2	вдоль стен А/В, прямая	от стены А, 1-й ряд вдоль неё	зазор от стены не задан
3	вдоль стен А/В, прямая	от стены А, 1-й ряд вдоль неё	зазор от стены не задан
4	вдоль стен А/В, прямая	от стены А, 1-й ряд вдоль неё	зазор от стены не задан
5	вдоль стен А/В, прямая	от стены А, 1-й ряд вдоль неё	зазор от стены не задан
6	вдоль стен А/В, прямая	от стены В, 1-й ряд вдоль неё	зазор от стены не задан
7	прямая, сетка 600×600, шов 2	ось X 1516 от Г; ось Y 1346 от А	X 311 / 311; Y 442 / 442
8	плитка	раскладка плиточника не задана	
9	прямая, сетка 600×600, шов 2	ось X 796 от Г; ось Y 1346 от А	X 494 / 494; Y 442 / 442

Спецификация плинтусов

Наименование	Помещения	Длина, м (с запасом)
Плинтус МДФ под покраску 80×16, крепление к стене, окраска в цвет Farrow & Ball No. 15	1, 3, 4, 5, 8	85
Плинтус МДФ под покраску 80×16, крепление к стене, окраска в цвет Tikkurila V503	2	10
SX165, h = 69 мм, крепление к стене, окраска в цвет Farrow & Ball No. 15	6	14


Примечания

1. За отметку ±0,000 принят чистый пол, не существующий (блок отметок). Площади — по чистым размерам помещений, м²; размеры — в мм.
2. Стык разнотипных покрытий — по оси дверного полотна (под полотном в закрытом положении); решение стыка — по ведомости стыков.
3. Пол санузлов ниже смежных помещений на 15 мм за счёт меньшей толщины стяжки (верх плиты общий — по экспликации полов); гидроизоляция по стяжке с заведением на стены не менее 200 мм (СП 29.13330.2011, п. 7.2), до облицовки — тест проливом и акт скрытых работ.
4. Трубопроводы в конструкции пола не прокладываются: пирог пола 49–64 мм не вмещает выпуски канализации с уклоном — выпуски К1 ведутся по стенам над чистым полом в коробах (лист 43).
5. Звукоизоляционный слой под стяжкой проектом не предусмотрен (стяжка по плите): приведённый уровень ударного шума перекрытия с полом Lnw не более 60 дБ (СП 51.13330.2011, табл. 2) подтвердить по данным дома; при превышении — плавающая стяжка по звукоизоляции с демпферной лентой по контуру и у стояков, пирог пересчитать.
6. Штучные покрытия (инженерная доска): направление — по стрелке; влажность основания по СМ не более 2,0 % (по ТУ изготовителя).
7. Ровность основания — просвет под 2-метровой рейкой не более 2 мм: пом. 1, 2, 3, 4, 5, 6 (инженерная доска), пом. 7, 8, 9 (керамогранит); проверить до укладки покрытия (СП 71.13330.2017, табл. 8.5).
8. Сетка на плитке — условная, в размер формата; точка старта и раскладка — по листу раскладки плитки.
9. Узор покрытия (заливка-код типа пола) прерывается под надписями — площадями помещений и отметками чистого пола.
10. Пироги полов — по экспликации полов: слои сверху вниз, толщины в мм; гидроизоляция мокрых зон — в пироге и в ведомости отделки; схема пола — без масштаба.


					Проект: Квартира с кабинетом — **М 1:75**
	Лист	№ док.	Подпись	Дата	
Дизайнер	Кырлан А.С.			04.11.26	План покрытий пола
					Стадия: П; Лист: 72; Листов: 127

выпуск 04.11.2026 № 627e1ac6ce · стр. 72 из 127

Фрагмент 1. Ванная (пом. 7). Пол 600×600, шов 2 мм, М 1:40

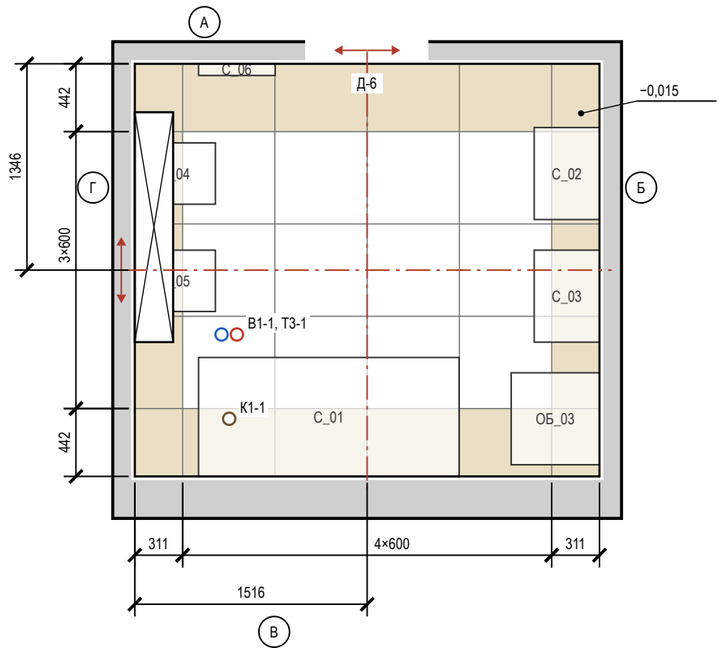

Фрагмент 2. Санузел гостевой (пом. 9). Пол 600×600, шов 2 мм, М 1:40

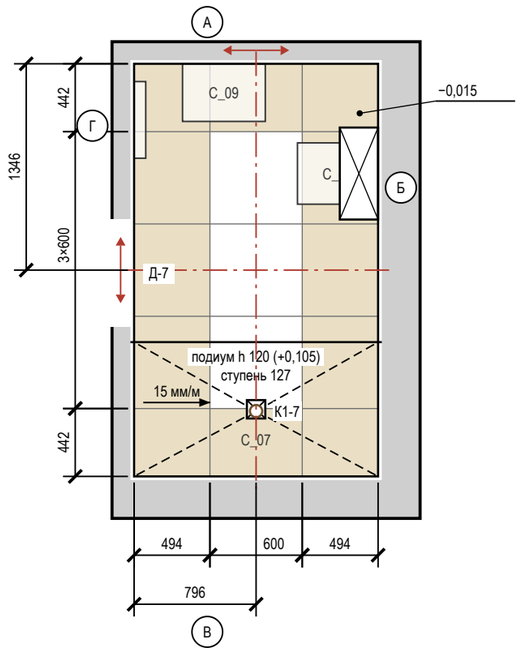

Условные обозначения

- плитка целая; тонкая линия — шов
- плитка с подрезкой (размер — на цепочке)
- ось старта; стрелки — направление укладки
- сантехприбор: габарит, высота по практике
- короб инсталляции: плитка пола — до короба
- трап / лоток в полу
- направление уклона К1 / пола: Ø, мм на 1 м
- край подиума; штрих — конверт к трапу
- вывод В1 (код — в ведомости привязок)
- вывод Т3 (код — в ведомости привязок)
- вывод К1 (код — в ведомости привязок)
- отметка чистого пола на полке выноски, м
- А — обозначение стены А–Г (как на развёртках)

Ведомость плитки

Помещение, поверхность	Плитка, код	Формат	Шов	S, м²	Целых	Подр.	С запасом
Ванная, пол	аналог: керамогранит под травертин	600×600	2	8,44	12	18	33
Ванная, стены А–Г	A8UZ	600×1200	2	26,96	9	55	72
Ванная, короб инсталляции	A8UZ	600×1200	2	2,77	1	7	9
Санузел гостевой, пол	аналог: керамогранит под травертин	600×600	2	4,49	3	13	18
Санузел гостевой, стены А–Г	A8UZ	600×1200	2	20,72	4	42	52
Санузел гостевой, короб инсталляции	A8UZ	600×1200	2	1,47	1	3	5
Прихожая, пол	A8UZ	600×1200	2	7,89	3	12	17
Кухня-гостиная, фартук (ст. А)	аналог: керамогранит под травертин, матовый	1200×600	2	0,70	0	2	3
Итого 600×600				12,93	15	31	51
Итого 600×1200				**60,51**	**18**	**121**	**158**

Ведомость материалов


Материал	Класс, код	Норма расхода	Кол-во
Затирка	CG2WA Mapei Ultracolor Plus 132	(a+b)/ab·шов·t·1,6	5,3 кг
Затирка	CG2WA	(a+b)/ab·шов·t·1,6	0,7 кг
Клей	C2 TE S1 Ceresit CM 17	1,5 кг/м²·мм, слой 5	521 кг (21 меш.)
Клей	C2 TE S1	1,5 кг/м²·мм, слой 5	70 кг (3 меш.)
Гидроизоляция	обмазочная, 2 слоя: пол, стены по периметру и зоны замачивания	по ТУ	33,0 м²
Демпф. лента	по периметру пола из плитки		28,0 м

Примечания


1. Раскладка от чистовых размеров: стены санузлов теряют 10 + 5 + 9 = 24 мм на сторону (штукатурка, клей, плитка); подрезки — чистые, без шва.
2. Старт — от центра помещения (штрихпунктир, стрелки — направление укладки); размер старта — от чистовых стен Г и А.
3. Раскладка пола «Прихожая» и фартука «Кухня-гостиная» — на листе «Раскладка плитки. Прихожая. Фартук кухни».
4. Калибр партии не задан — до укладки замерить (рабочий размер W, ГОСТ 13996-2019) и пересчитать подрезки.
5. Количество: целые по раскладке + по одной на подрезку, запас 10 %; один артикул — одна партия и тон. Исключены поддон, короб, проёмы и места за коробом; S — по чистым граням: стены нетто = зона облицовки по ведомости отделки − место за коробом инсталляции 2,52 м² (плитку за коробом не кладут), короб — отдельной строкой.
6. Клей C2 TE S1 Ceresit CM 17; C2 TE S1 (ГОСТ Р 56387-2018), затирка CG2WA Mapei Ultracolor Plus 132; CG2WA; расход — по ТУ выбранной марки.
7. Гидроизоляция: пол и стены 200 мм от ЧП; над ванной — до 2000 и 300 мм за борт (пом. 7), у душа — на всю высоту стен душевой зоны и 500 мм за край душевой зоны (пом. 9) (см. развёртки); акт скрытых работ, пролив 24 ч.
8. Подиум душа С_07 (пом. 9): h 120 у трапа, решётка +0,105; верх — плиткой пола той же раскладки, уклон 15 мм/м к трапу, подрезка по линиям конверта; ступень по краю 127, грань 1592 × 127 = 0,20 м² (+1 шт. в подрезках), угол профилем; гидроизоляция 2 сл. — по плите под подиумом, по верху и грани (узел 1 ВК); предложение, до согласования не выполнять.
9. Швы пола совмещены со швами стены А; по периметру — демпферная лента.
10. Отметка чистого пола −0,015, порог 15 мм; стык с соседним покрытием — по оси полотна двери.

					Проект: Квартира с кабинетом	**М 1:40**
	Лист	№ док.	Подпись	Дата		
Дизайнер	Кырлан А.С.			04.11.26	Раскладка плитки. Планы полов	Стадия: П; Лист: 73; Листов: 127

Фрагмент 1. Прихожая (пом. 8). Пол 600×1200, шов 2 мм, М 1:20

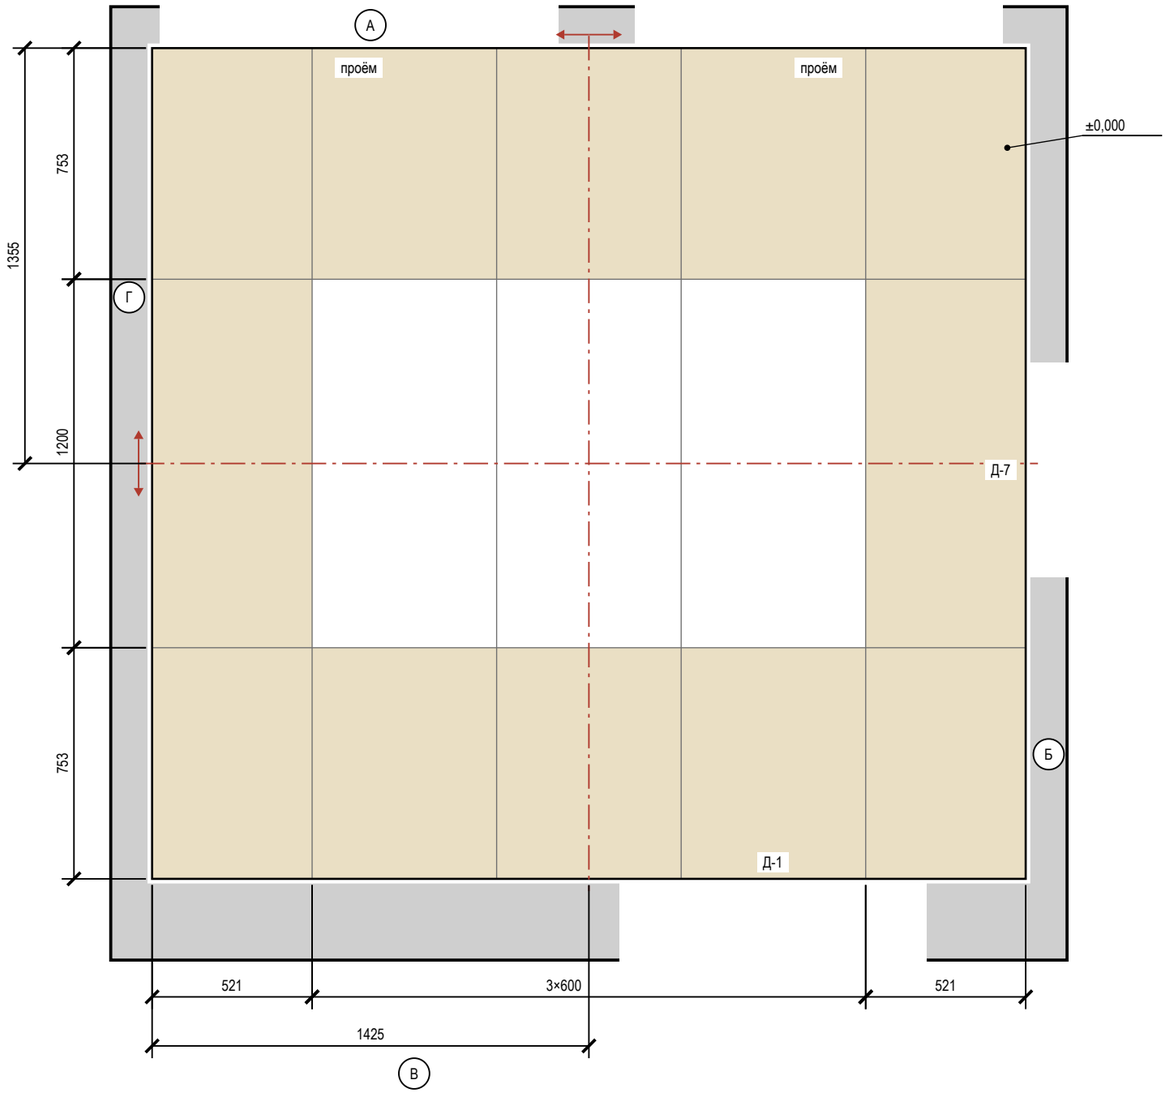

Фрагмент 2. Кухня-гостиная (пом. 4), фартук, стена А. 1200×600, шов 2 мм, М 1:20

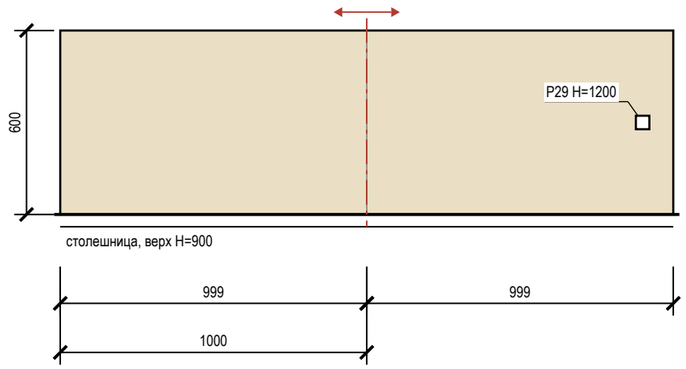

Условные обозначения

- плитка целая; тонкая линия — шов
- плитка с подрезкой (размер — на цепочке)
- ось старта; стрелки — направление укладки
- электроточка: марка и H — по листам ЭОМ
- столешница (верх)
- навесной шкаф над фартуком
- отметка чистого пола на полке выноски, м
- А — обозначение стены А–Г (как на развёртках)

Подсчёт плитки


Поверхность	Формат	S, м²	Целых	Подр.	С запасом
Прихожая, пол	600×1200	7,89	3	12	17
Кухня-гостиная, фартук (ст. А)	1200×600	0,70	0	2	3

Примечания

1. Прихожая: керамогранит 600×1200, длинная сторона — вдоль стен Б и Г, шов 2 мм, прямая раскладка от центра. Стены окрашены: раскладка от чистового контура минус штукатурка и шпаклёвка 15 мм на сторону (принято); подрезки 521 / 753 мм, срез — под плинтус.
2. Прихожая: деформационный зазор по периметру 8–10 мм под плинтусом; в проёмах — стык с соседним покрытием по оси полотна двери. Клей C2 TE S1, затирка CG2WA.
3. Фартук, Кухня-гостиная: 1200×600 горизонтально, шов 2 мм; зоны 2000 мм — 900…1500 (от столешницы до низа навесного шкафа, без шкафа — 600 мм). Старт от центра участка, подрезки 999 мм. Площадь 0,70 м² — как в ведомости отделки.
4. Фартук — после монтажа столешницы, низ на 2–3 мм выше неё, шов со столешницей — санитарный герметик; навесные шкафы — после фартука. Торцы у пенала и стены — профиль или запил 45°.
5. Клей, затирка и итог по форматам — в ведомостях листа «Раскладка плитки. Планы полов».

					Проект: Квартира с кабинетом	М 1:20
	Лист	№ док.	Подпись	Дата		
Дизайнер	Кырлан А.С.			04.11.26	Раскладка плитки. Прихожая. Фартук кухни	Стадия: П; Лист: 74; Листов: 127


Развёртка стены А

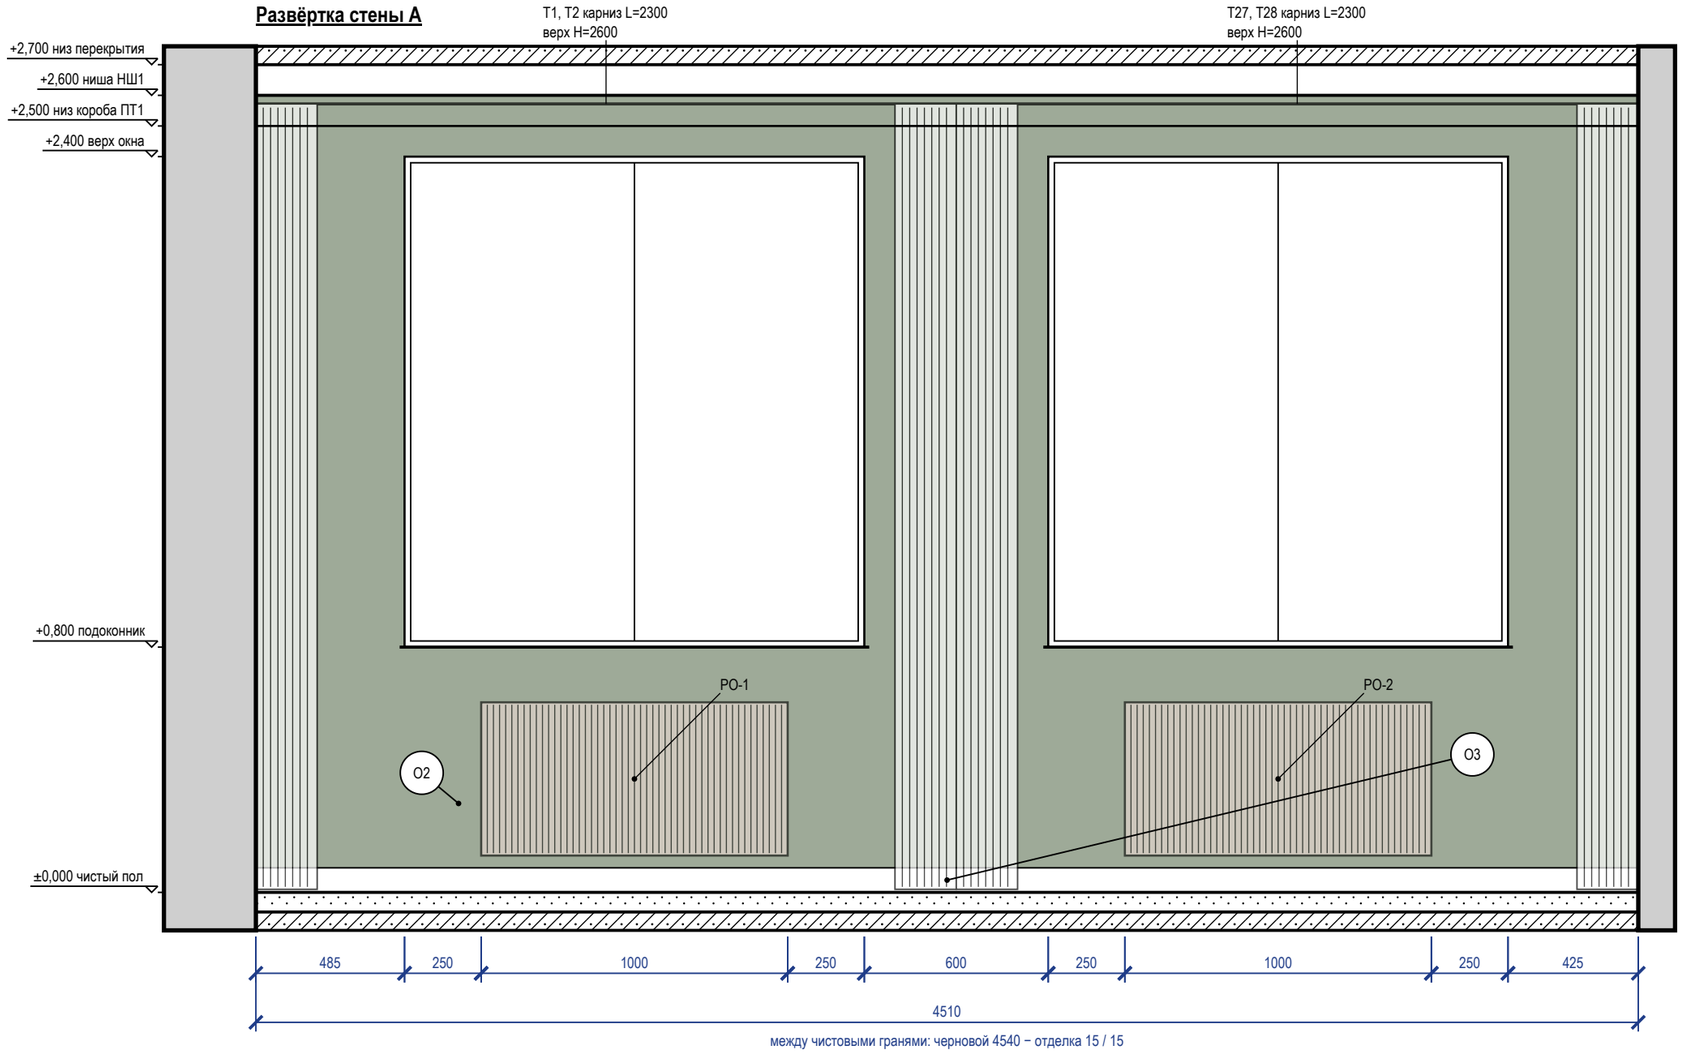

Визуализация этой стены — лист 4



Схема развёрток (М 1:100)

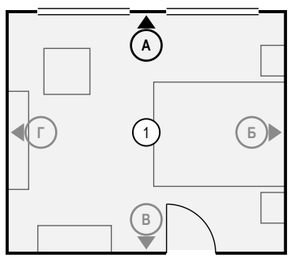

Ведомость отделки (на листе)

Марка	Поверхность	Материал, изделие	Цвет, код	Кол.
О2	акцентная стена	окраска, Farrow & Ball Modern Emulsion, матовая, подготовка Q3	Farrow & Ball No. 34 «Calke Green традиционный шалфей»	6,9 м²
О3	плинтус	плинтус МДФ, h 80 мм, аналог: плинтус МДФ под покраску 80×16	Farrow & Ball No. 15 «Bone — мягкий каменно-серый с зеленцой»	4,5 м
О4	потолок	окраска, Tikkurila Anti-Reflex 2, глубокоматовая, подготовка Q3	Tikkurila V503 «Winter»	17,9 м²

Примечания

1. Размеры — в мм от чистовых поверхностей стен; условные обозначения и общие указания — лист 27.
2. Карнизы (шины) — по ведомости текстиля декоратора: длина L и верх H на развёртке — те же числа, что в ведомости; крепление — до окраски потолка.
3. Потолок — у каждой стены свой, по плану потолков (НШ1, ПТ1); ступени — зоной, кромка короба перед нишей — тонкой линией; в поле потолка: ПТ2 +2,600.
4. Карниз T1, T2: по ведомости текстиля шина L=2300 мм, а от её начала до чистового угла стены — 2285 мм: шина не встаёт, длину согласовать с декоратором до заказа.
5. Карниз T27, T28: по ведомости текстиля шина L=2300 мм, а от её начала до чистового угла стены — 2225 мм: шина не встаёт, длину согласовать с декоратором до заказа.

					Проект: Квартира с кабинетом	М 1:20
	Лист	№ док.	Подпись	Дата		
Дизайнер	Кырлан А.С.			04.11.26	Развёртка стены А. Спальня (пом. 1)	Стадия: П; Лист: 75; Листов: 127

Развёртка стены Б


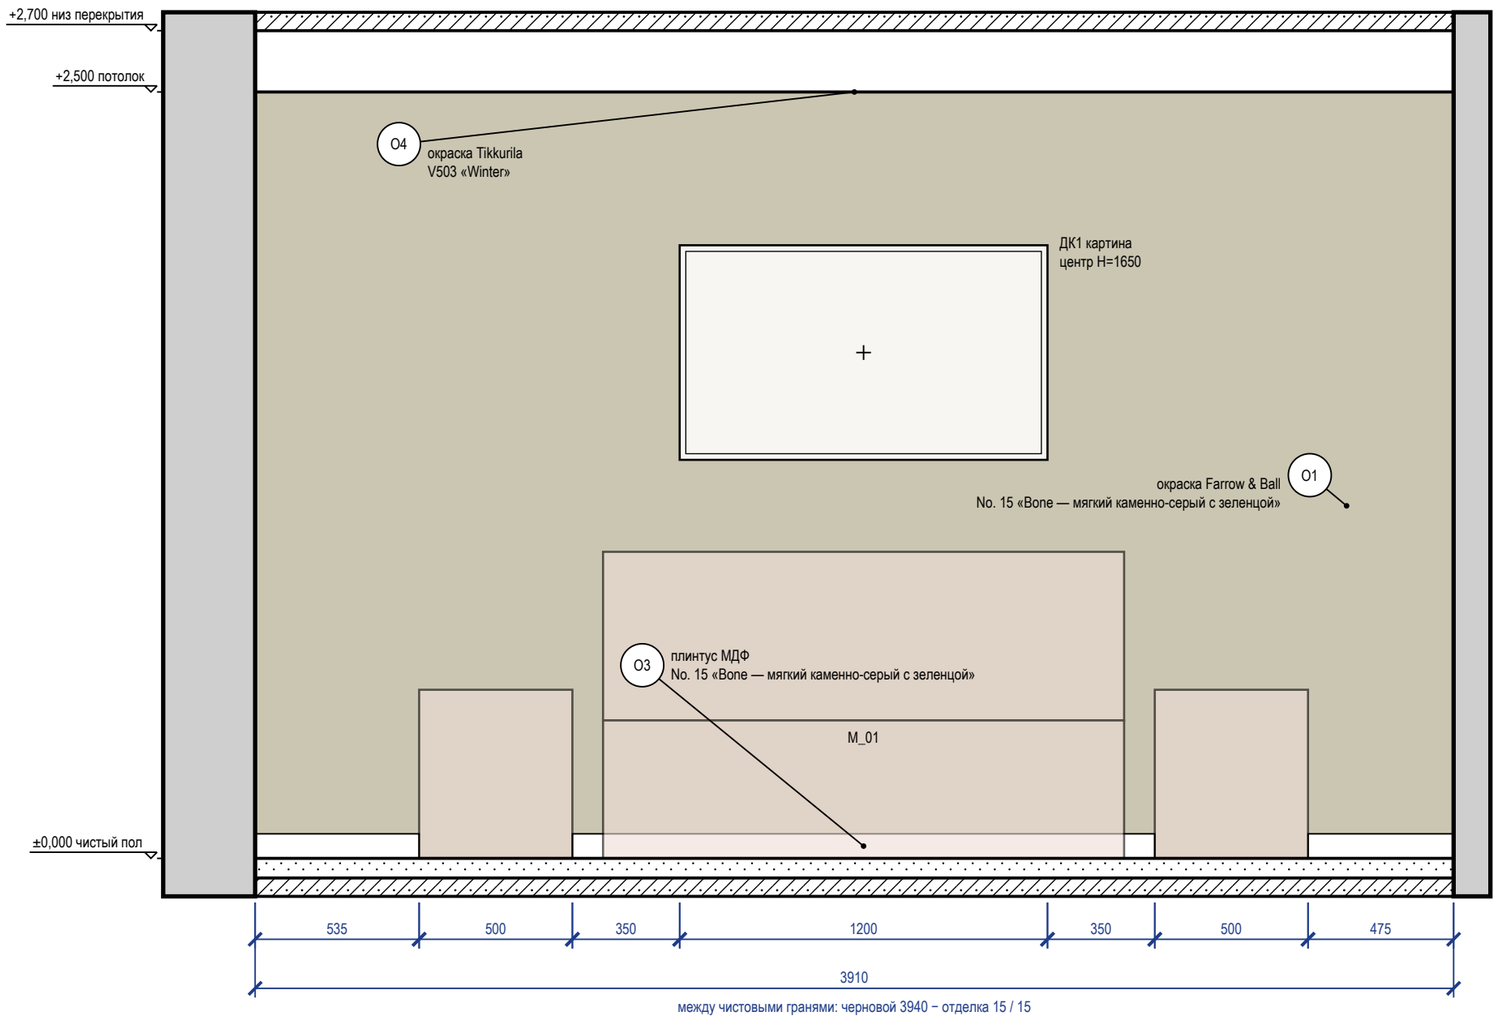


Схема развёрток (М 1:100)

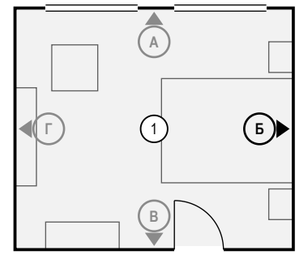

Ведомость отделки (на листе)

Марка	Поверхность	Материал, изделие	Цвет, код	Кол.
О1	стены	окраска, Farrow & Ball Modern Emulsion, матовая, подготовка Q3	Farrow & Ball No. 15 «Bone — мягкий каменно-серый с зеленцой»	9,8 м²
О3	плинтус	плинтус МДФ, h 80 мм, аналог: плинтус МДФ под покраску 80×16	Farrow & Ball No. 15 «Bone — мягкий каменно-серый с зеленцой»	2,9 м
О4	потолок	окраска, Tikkurila Anti-Reflex 2, глубокоматовая, подготовка Q3	Tikkurila V503 «Winter»	17,9 м²

Визуализация этой стены — лист 5



Примечания

1. Размеры — в мм от чистовых поверхностей стен; условные обозначения и общие указания — лист 27.
2. Стена Б показана двумя видами: здесь — архитектурная развёртка (мебель, отделка, проёмы, высоты), электроточки и выводы ВК с привязками и таблицей — на листе 77 («Привязки»).
3. Картины и зеркала крепить к основанию по паспорту изделия (закладные и анкеры — в перечне скрытых работ); крест — ось центра предмета.
4. Потолок — у каждой стены свой, по плану потолков (ПТ1); ступени — зоной, кромка короба перед нишей — тонкой линией; в поле потолка: ПТ2 +2,600.

					Проект: Квартира с кабинетом	М 1:20
	Лист	№ док.	Подпись	Дата		
Дизайнер	Кырлан А.С.			04.11.26	Развёртка стены Б. Спальня (пом. 1)	Стадия: П; Лист: 76; Листов: 127

Развёртка стены Б: электроточки и выводы

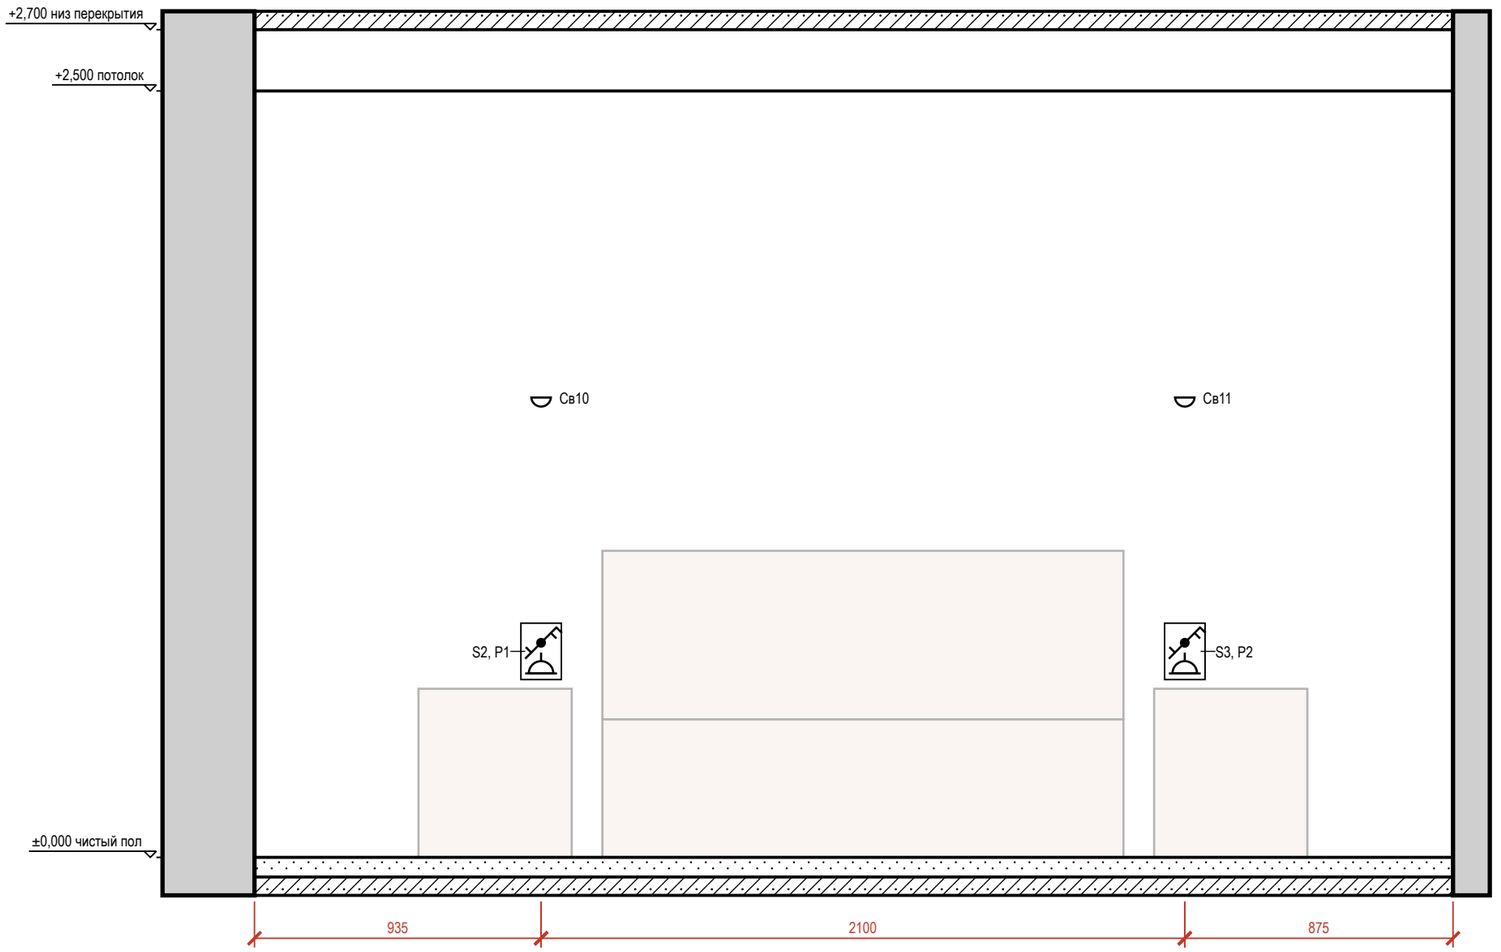



Таблица привязок электроточек и выводов

Марка	Назначение	От угла, мм	H от пола, мм	Примечание
P1	розетка: у кровати	935	600	гр. 4
S2	выключатель	935	700	гр. 1
Св10	светильник настенный	935	1500	гр. 1
P2	розетка: у кровати	3035	600	гр. 4
S3	выключатель	3035	700	гр. 1
Св11	светильник настенный	3035	1500	гр. 1

Условные обозначения

- розетка с заземляющим контактом; у знака — марка, ×N постов в рамке, гр. — группа щита, H — высота оси, мм
- выключатель одноклавишный
- выключатель двухклавишный (флажков — по числу клавиш)
- выключатель с проходной или перекрёстной клавишей (обратный флажок); тип клавиши — в подписи
- светильник настенный (бра), H — высота оси
- привязки точек и выводов от угла и от пола, мм
- марка развёртки: буква стены, стрелка — взгляд

Схема развёрток (М 1:50)

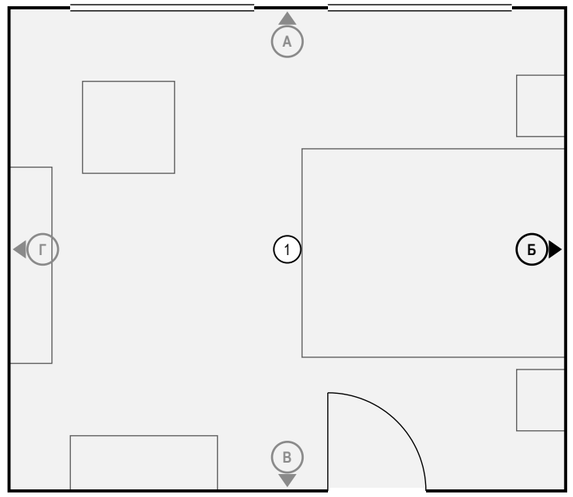

Примечания

1. Вид «Привязки» стены Б — электроточки и выводы ВК; архитектурная развёртка (мебель, отделка, проёмы, высоты) — на листе 76. Мебель и приборы — подложкой для ориентира; их марки и обозначения мебели, проёмов и стен — там же.
2. Привязки — в мм: по горизонтали от левого чистового угла стены до оси изделия, H — от чистого пола до оси; все точки — в таблице привязок. Красная цепочка — привязки по осям; точки ближе 120 мм одна к другой в цепочку не дробятся — их привязки только в таблице.
3. У знака — марка электроточки (P — розетка, S — выключатель, Св — светильник, ЭВ — вывод кабеля); условные обозначения и общие указания — лист 27.

					Проект: Квартира с кабинетом	М 1:20
	Лист	№ док.	Подпись	Дата		
Дизайнер	Кырлан А.С.			04.11.26	Привязки электроточек, стена Б. Спальня (пом. 1)	Стадия: П; Лист: 77; Листов: 127

Развёртка стены В


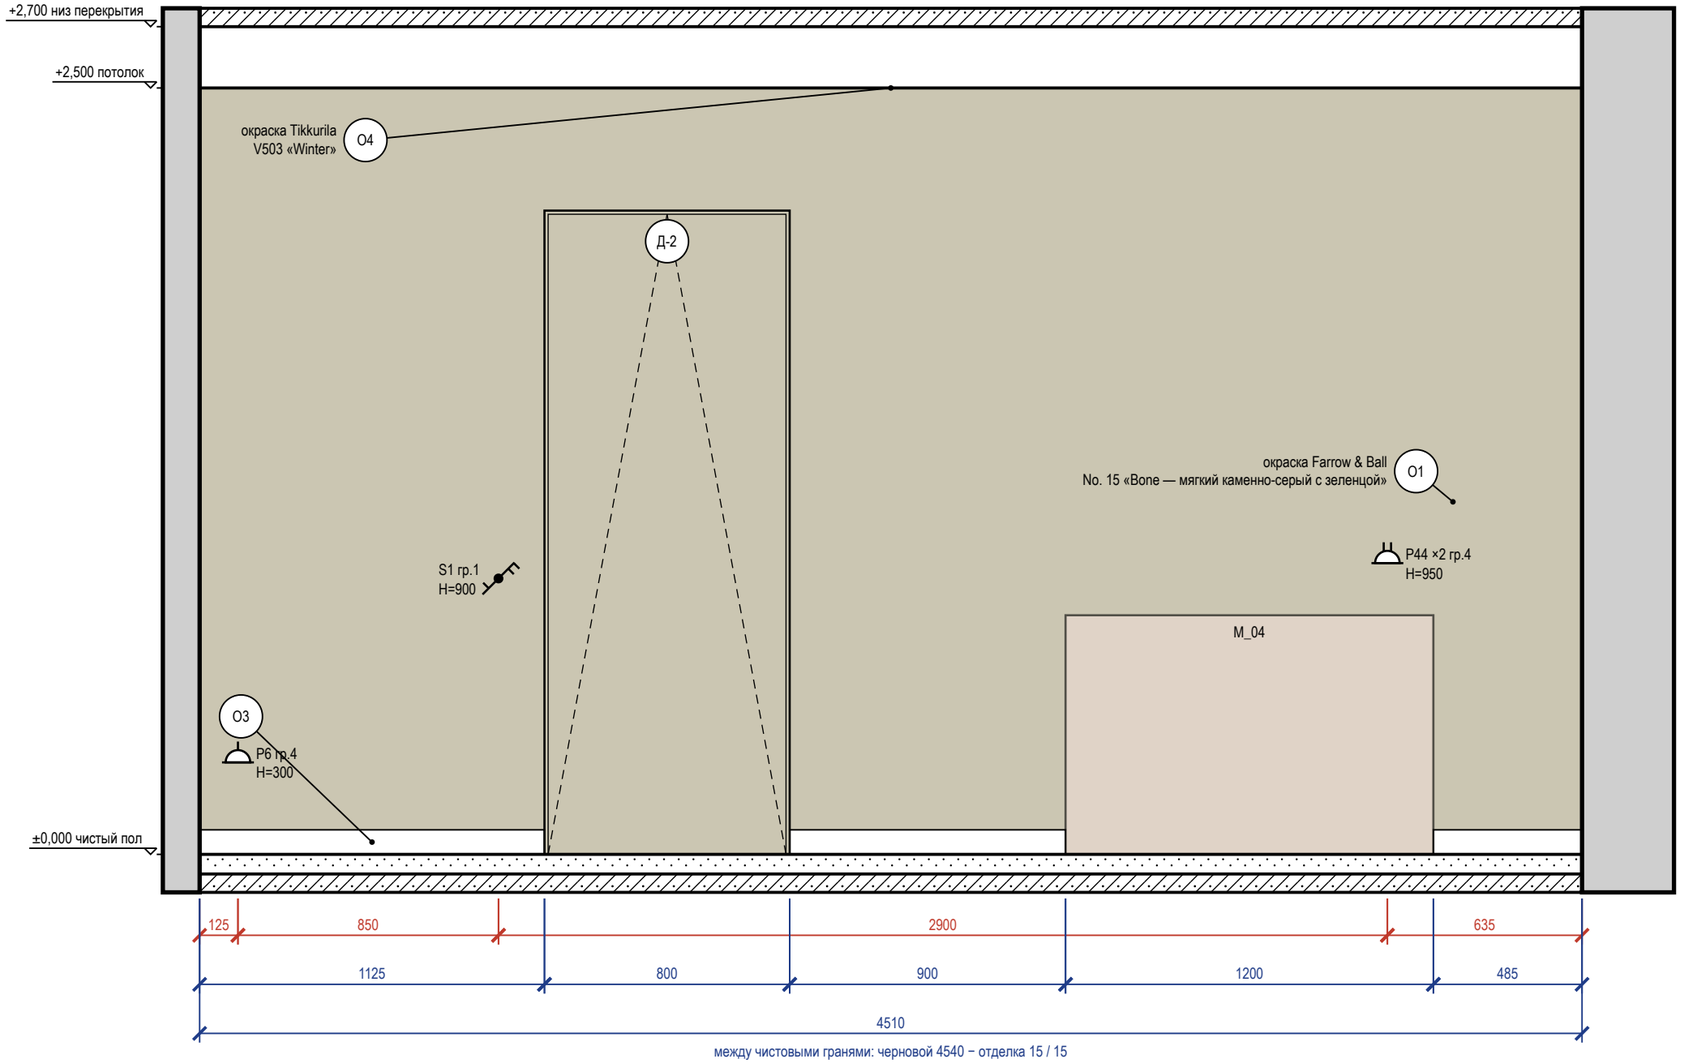


Схема развёрток (М 1:100)

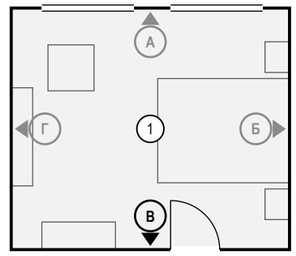

Ведомость отделки (на листе)


Марка	Поверхность	Материал, изделие	Цвет, код	Кол.
О1	стены	окраска, Farrow & Ball Modern Emulsion, матовая, подготовка Q3	Farrow & Ball No. 15 «Bone — мягкий каменно-серый с зеленцой»	9,6 м²
О3	плинтус	плинтус МДФ, h 80 мм, аналог: плинтус МДФ под покраску 80×16	Farrow & Ball No. 15 «Bone — мягкий каменно-серый с зеленцой»	2,5 м
О4	потолок	окраска, Tikkurila Anti-Reflex 2, глубокоматовая, подготовка Q3	Tikkurila V503 «Winter»	17,9 м²

Примечания

1. Размеры — в мм от чистовых поверхностей стен; условные обозначения и общие указания — лист 27.
2. Двери скрытого монтажа — полотно в плоскости стены, отделка стены по полотну, плинтус прерывается у короба (узел — на листе узлов).
3. Потолок — у каждой стены свой, по плану потолков (ПТ1); ступени — зоной, кромка короба перед нишей — тонкой линией; в поле потолка: ПТ2 +2,600.


					Проект: Квартира с кабинетом	М 1:20
	Лист	№ док.	Подпись	Дата		
Дизайнер	Кырлан А.С.			04.11.26	Развёртка стены В. Спальня (пом. 1)	Стадия: П; Лист: 78; Листов: 127

Развёртка стены Г

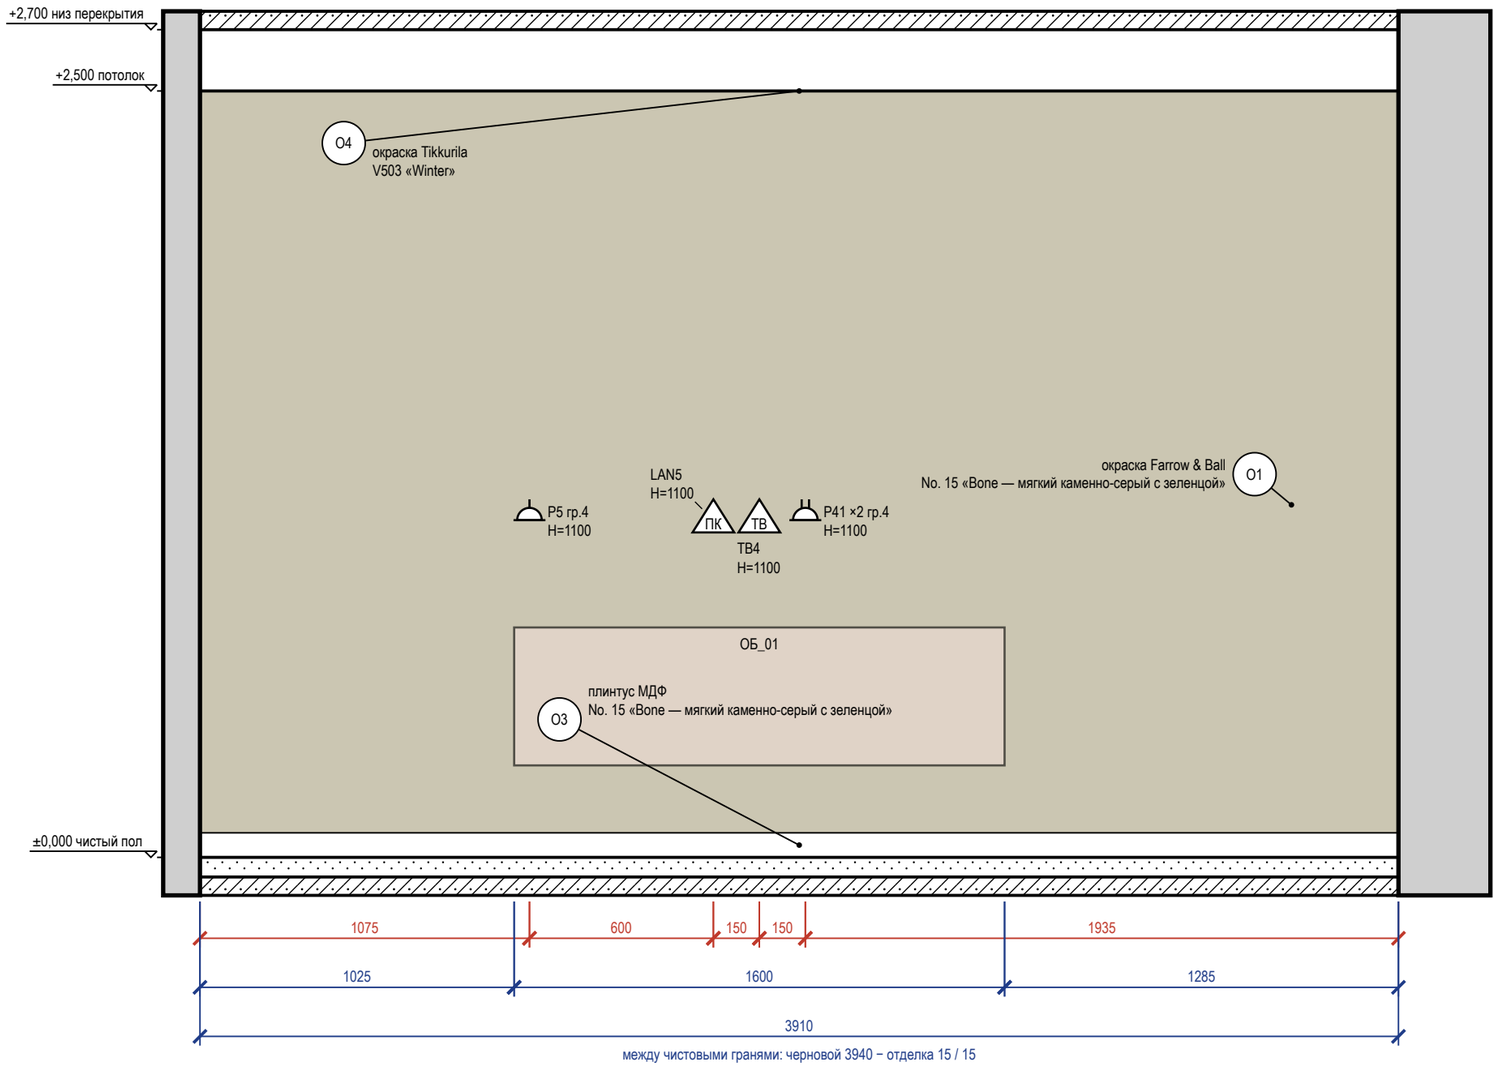

между чистовыми гранями: черновой 3940 − отделка 15 / 15

Схема развёрток (М 1:100)

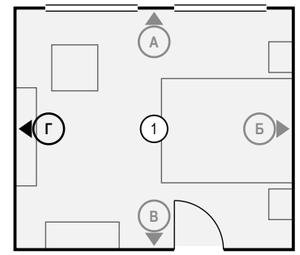

Ведомость отделки (на листе)

Марка	Поверхность	Материал, изделие	Цвет, код	Кол.
О1	стены	окраска, Farrow & Ball Modern Emulsion, матовая, подготовка Q3	Farrow & Ball No. 15 «Bone — мягкий каменно-серый с зеленцой»	9,8 м²
О3	плинтус	плинтус МДФ, h 80 мм, аналог: плинтус МДФ под покраску 80×16	Farrow & Ball No. 15 «Bone — мягкий каменно-серый с зеленцой»	3,9 м
О4	потолок	окраска, Tikkurila Anti-Reflex 2, глубокоматовая, подготовка Q3	Tikkurila V503 «Winter»	17,9 м²

Визуализация этой стены — лист 6




Примечания

1. Размеры — в мм от чистовых поверхностей стен; условные обозначения и общие указания — лист 27.
2. Потолок — у каждой стены свой, по плану потолков (ПТ1); ступени — зоной, кромка короба перед нишей — тонкой линией; в поле потолка: ПТ2 +2,600.

					Проект: Квартира с кабинетом — М 1:20
	Лист	№ док.	Подпись	Дата	Развёртка стены Г. Спальня (пом. 1)
Дизайнер	Кырлан А.С.			04.11.26	Стадия: П; Лист: 79; Листов: 127

Развёртка стены А

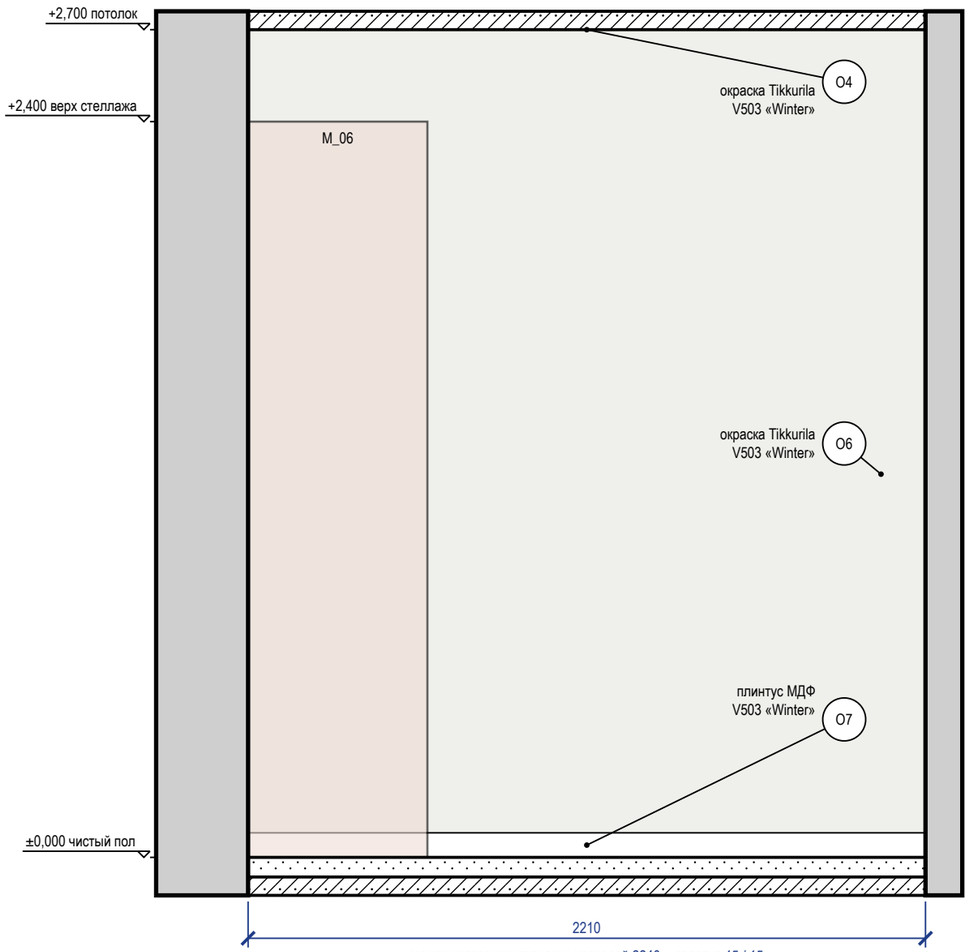

Развёртка стены Б


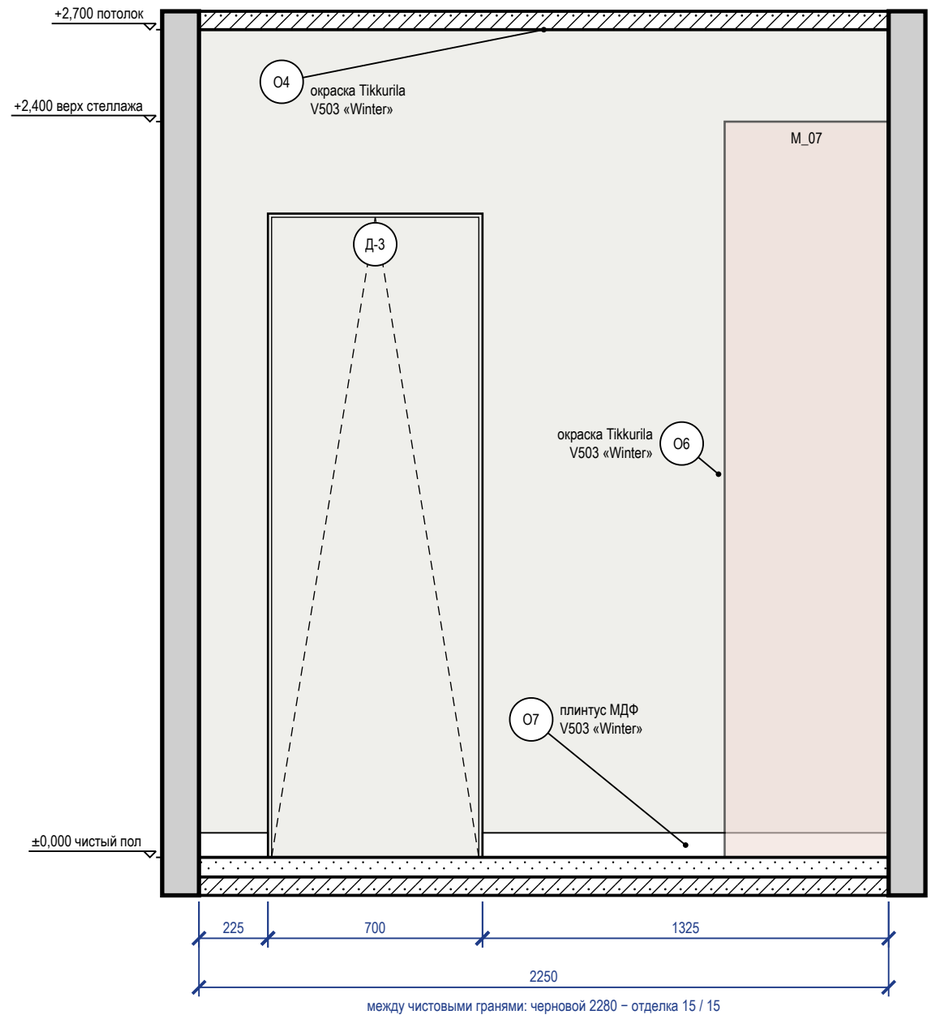


Схема развёрток (М 1:100)

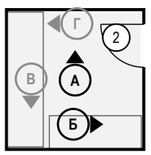

Ведомость отделки (на листе)


Марка	Поверхность	Материал, изделие	Цвет, код	Кол.
О4	потолок	окраска, Tikkurila Anti-Reflex 2, глубокоматовая, подготовка Q3	Tikkurila V503 «Winter»	5,1 м²
О6	стены	окраска, Tikkurila Harmony, матовая, подготовка Q3	Tikkurila V503 «Winter»	10,6 м²
О7	плинтус	плинтус МДФ, h 80 мм, аналог: плинтус МДФ под покраску 80×16	Tikkurila V503 «Winter»	3,8 м

Примечания

1. Размеры — в мм от чистовых поверхностей стен; условные обозначения и общие указания — лист 27.
2. Двери скрытого монтажа — полотно в плоскости стены, отделка стены по полотну, плинтус прерывается у короба (узел — на листе узлов).

					Проект: Квартира с кабинетом	М 1:20
	Лист	№ док.	Подпись	Дата	Развёртки стен А, Б. Гардеробная-постирочная (пом. 2)	Стадия: П; Лист: 80; Листов: 127
Дизайнер	Кырлан А.С.			04.11.26		

Развёртка стены В

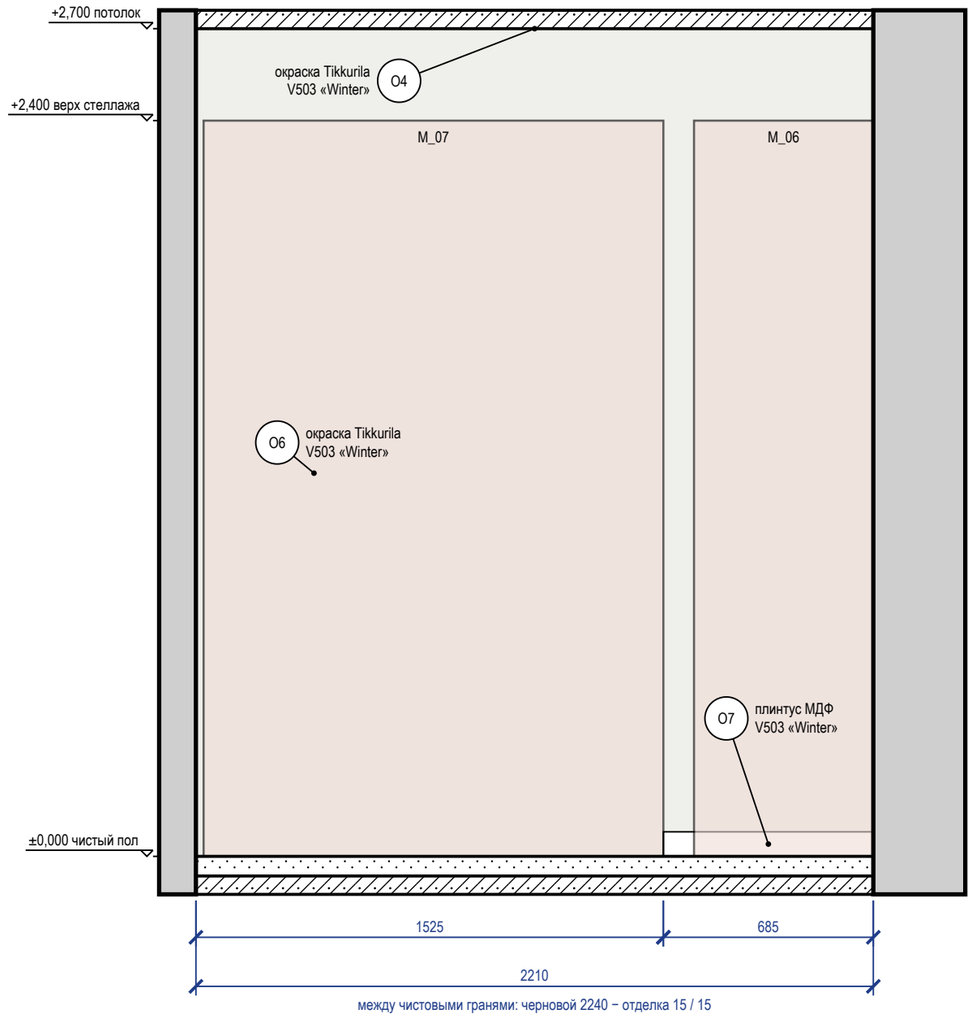

Развёртка стены Г


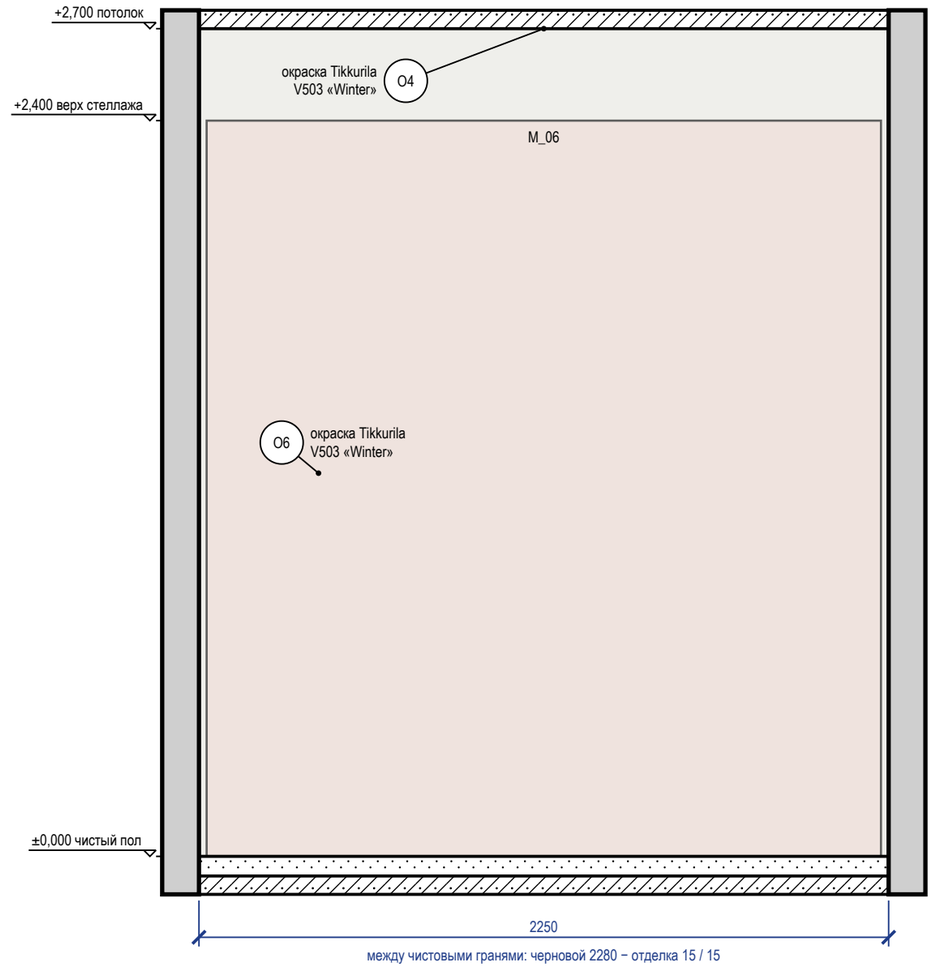


Схема развёрток (М 1:100)

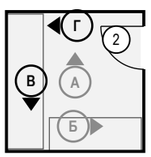

Ведомость отделки (на листе)

Марка	Поверхность	Материал, изделие	Цвет, код	Кол.
O4	потолок	окраска, Tikkurila Anti-Reflex 2, глубокоматовая, подготовка Q3	Tikkurila V503 «Winter»	5,1 м²
O6	стены	окраска, Tikkurila Harmony, матовая, подготовка Q3	Tikkurila V503 «Winter»	12 м²
O7	плинтус	плинтус МДФ, h 80 мм, аналог: плинтус МДФ под покраску 80×16	Tikkurila V503 «Winter»	0,7 м

Визуализация этой стены — лист 7



Примечания

1. Размеры — в мм от чистовых поверхностей стен; условные обозначения и общие указания — лист 27.

					Проект: Квартира с кабинетом	М 1:20
	Лист	№ док.	Подпись	Дата		
Дизайнер	Кырлан А.С.			04.11.26	Развёртки стен В, Г. Гардеробная-постирочная (пом. 2)	Стадия: П; Лист: 81; Листов: 127

выпуск 04.11.2026 № 627e1ac6ce · стр. 81 из 127

Развёртка стены А


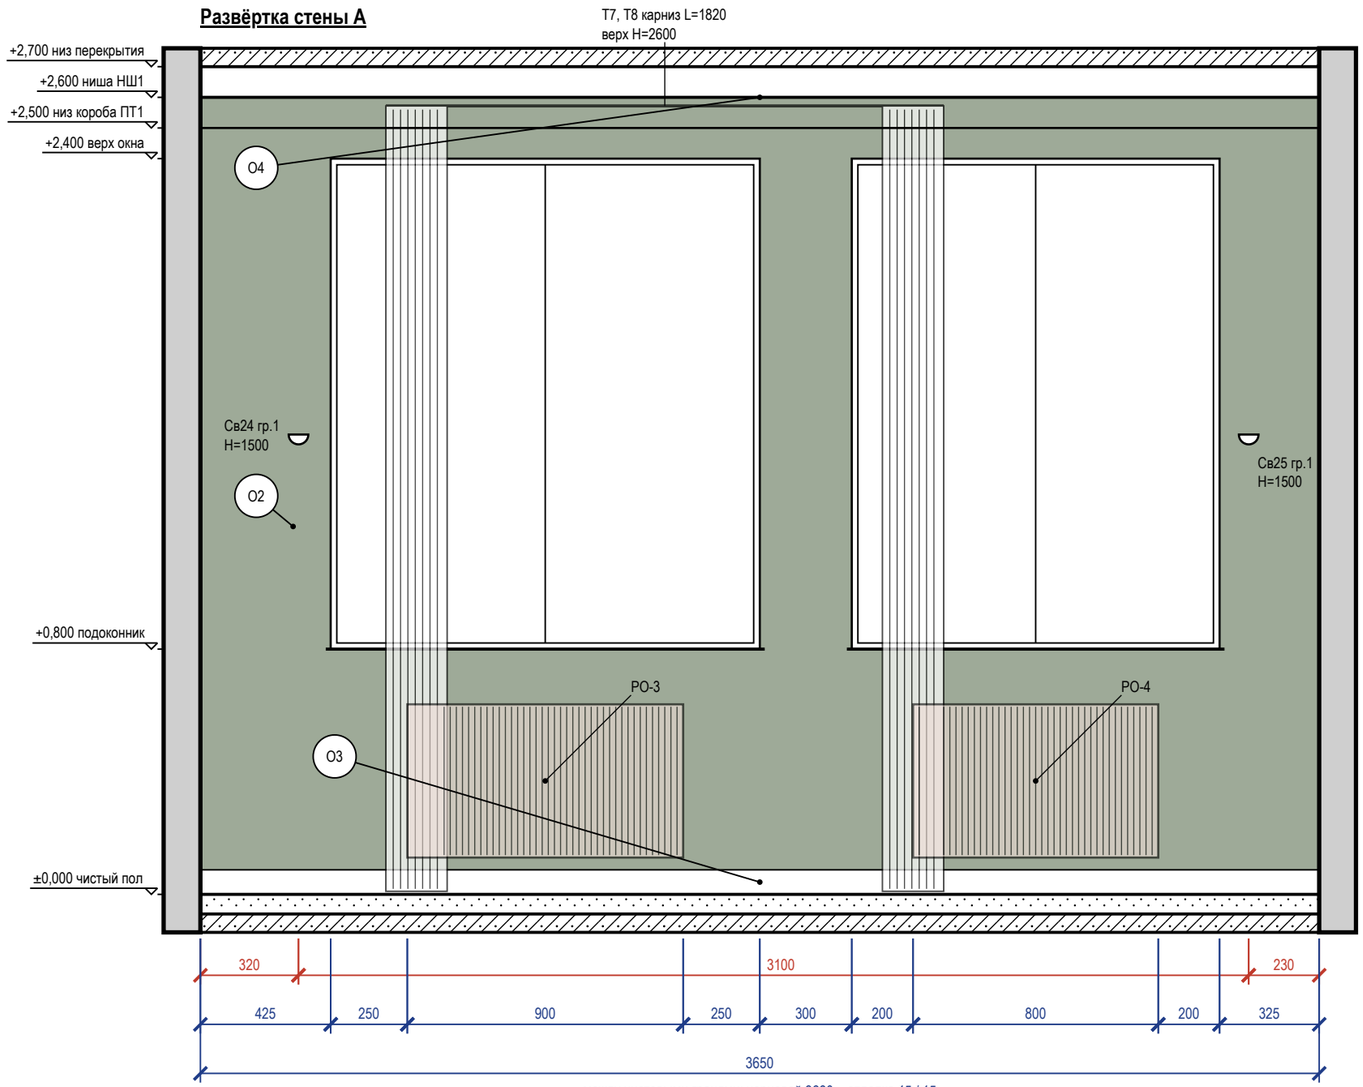


Схема развёрток (М 1:100)

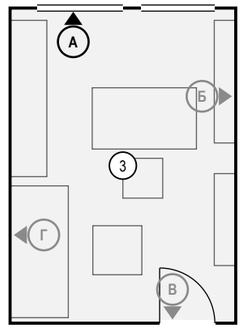

Ведомость отделки (на листе)

Марка	Поверхность	Материал, изделие	Цвет, код	Кол.
О2	акцентная стена	окраска, Farrow & Ball Modern Emulsion, матовая, подготовка Q3	Farrow & Ball No. 34 «Calke Green традиционный шалфей»	5,3 м²
О3	плинтус	плинтус МДФ, h 80 мм, аналог: плинтус МДФ под покраску 80×16	Farrow & Ball No. 15 «Bone — мягкий каменно-серый с зеленцой»	3,6 м
О4	потолок	окраска, Tikkurila Anti-Reflex 2, глубокоматовая, подготовка Q3	Tikkurila V503 «Winter»	18,9 м²

Визуализация этой стены — лист 8



Примечания

1. Размеры — в мм от чистовых поверхностей стен; условные обозначения и общие указания — лист 27.
2. Карнизы (шины) — по ведомости текстиля декоратора: длина L и верх H на развёртке — те же числа, что в ведомости; крепление — до окраски потолка.
3. Потолок — у каждой стены свой, по плану потолков (НШ1, ПТ1); ступени — зоной, кромка короба перед нишей — тонкой линией; в поле потолка: ПТ2 +2,600.
4. Линии узора (швы плитки, складки штор, рёбра радиаторов) прерываются у знаков и выносок — просвет между линиями не менее 0,7 мм.

					Проект: Квартира с кабинетом	М 1:20
	Лист	№ док.	Подпись	Дата	Развёртка стены А. Кабинет (пом. 3)	Стадия: П; Лист: 82; Листов: 127
Дизайнер	Кырлан А.С.			04.11.26		

Развёртка стены Б


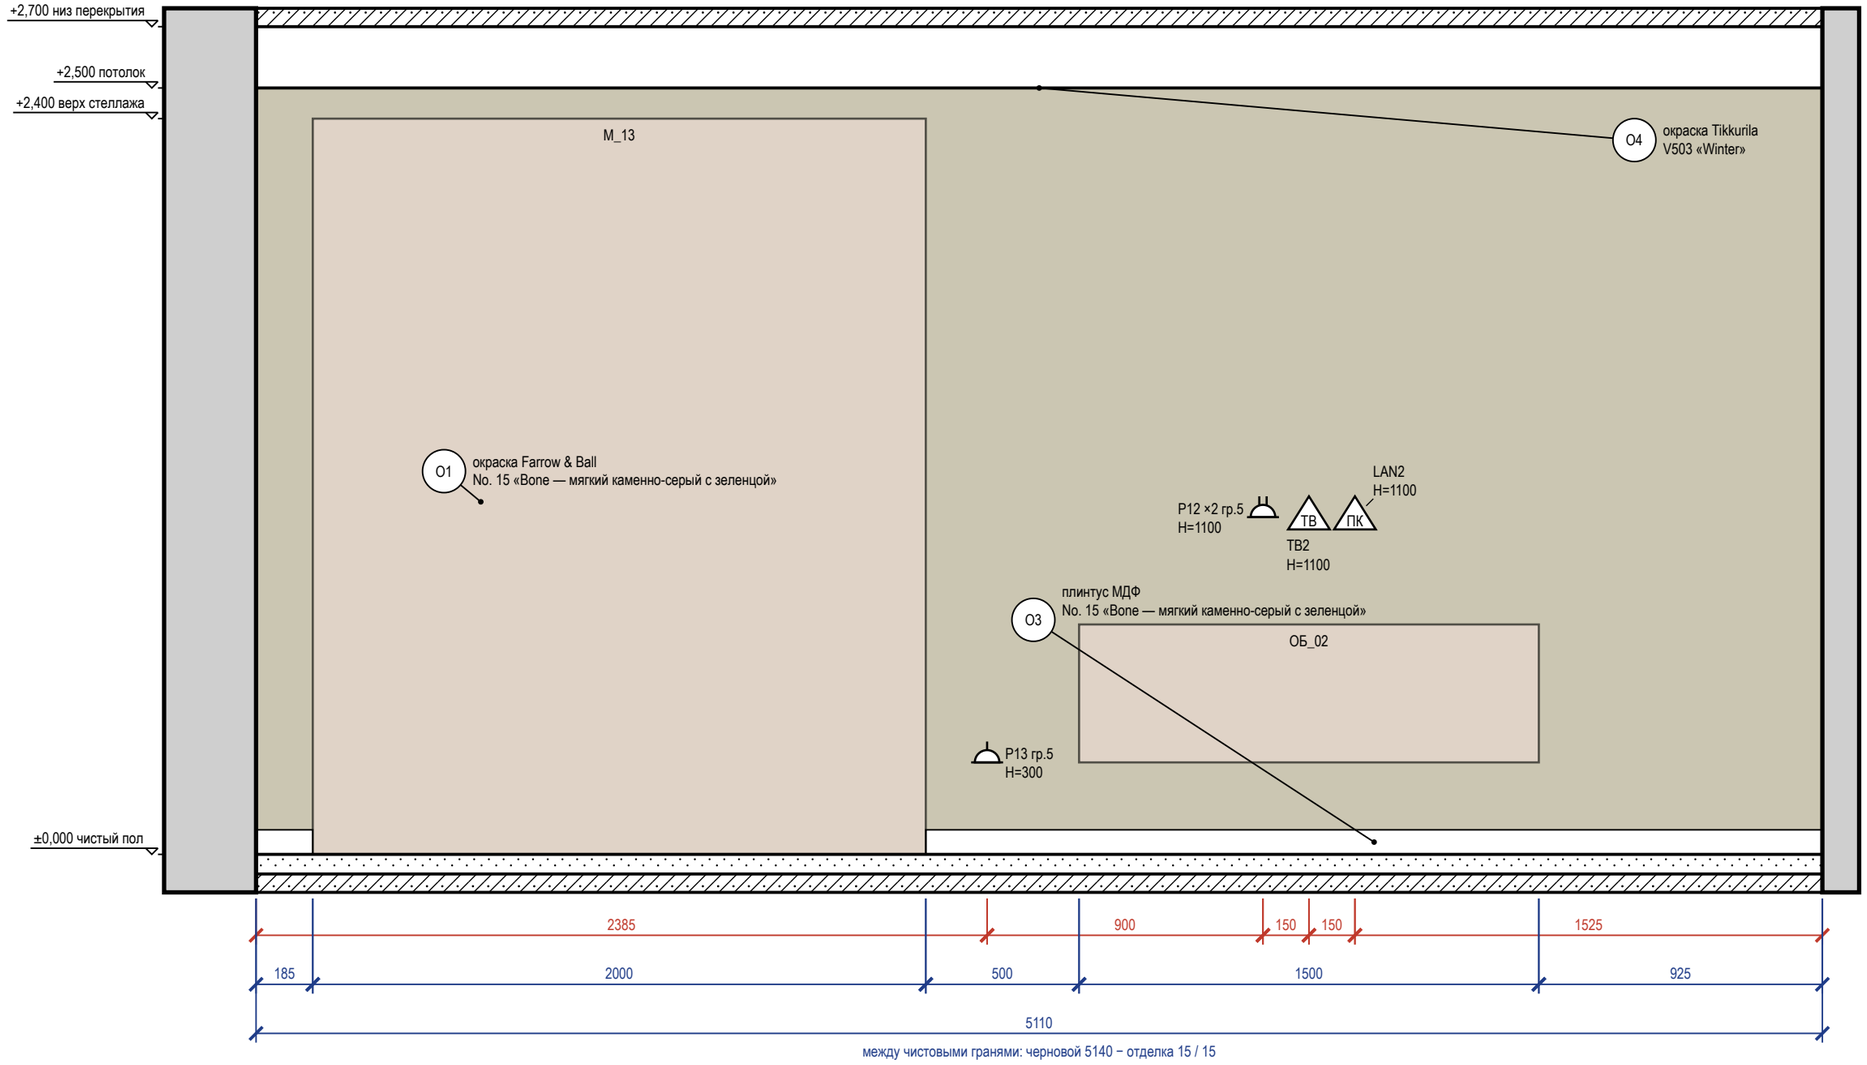


Схема развёрток (М 1:100)

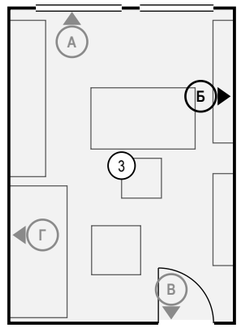

Ведомость отделки (на листе)

Марка	Поверхность	Материал, изделие	Цвет, код	Кол.
О1	стены	окраска, Farrow & Ball Modern Emulsion, матовая, подготовка Q3	Farrow & Ball No. 15 «Bone — мягкий каменно-серый с зеленцой»	12,8 м²
О3	плинтус	плинтус МДФ, h 80 мм, аналог: плинтус МДФ под покраску 80×16	Farrow & Ball No. 15 «Bone — мягкий каменно-серый с зеленцой»	3,1 м
О4	потолок	окраска, Tikkurila Anti-Reflex 2, глубокоматовая, подготовка Q3	Tikkurila V503 «Winter»	18,9 м²

Визуализация этой стены — лист 9



Примечания

1. Размеры — в мм от чистовых поверхностей стен; условные обозначения и общие указания — лист 27.
2. Потолок — у каждой стены свой, по плану потолков (ПТ1); ступени — зоной, кромка короба перед нишей — тонкой линией; в поле потолка: ПТ2 +2,600.

	Лист	№ док.	Подпись	Дата
Дизайнер	Кырлан А.С.			04.11.26


Проект: Квартира с кабинетом — М 1:20

Развёртка стены Б. Кабинет (пом. 3)

Стадия	Лист	Листов
П	83	127


выпуск 04.11.2026 № 627e1ac6ce · стр. 83 из 127

Развёртка стены В

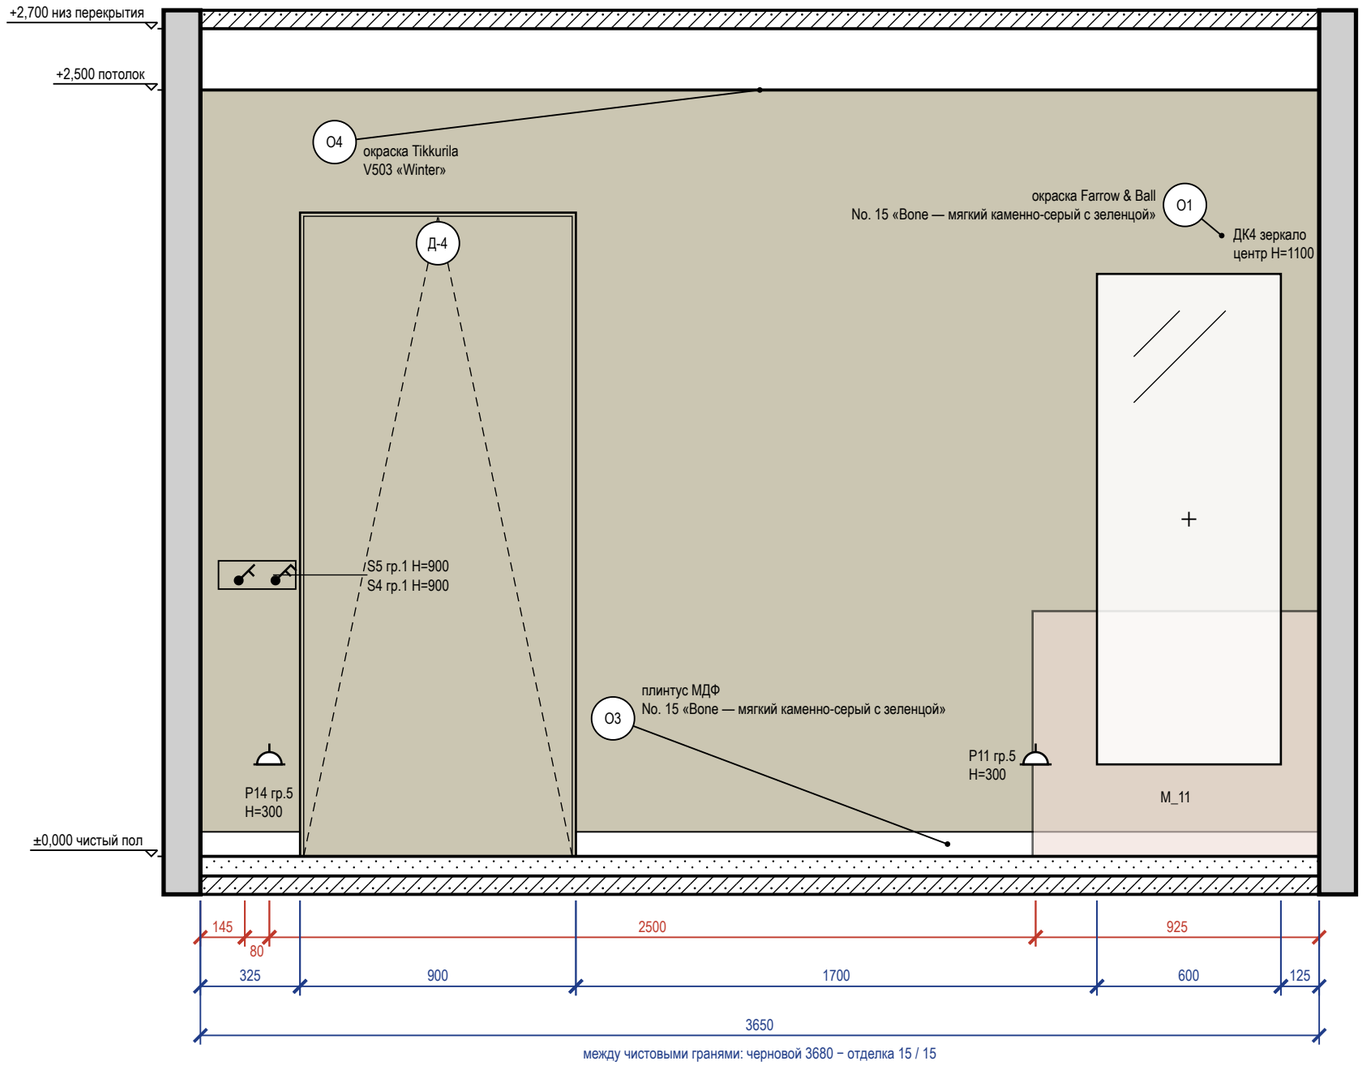

между чистовыми гранями: черновой 3680 − отделка 15 / 15

Схема развёрток (М 1:100)

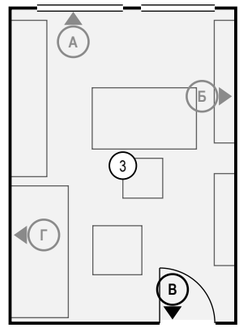

Ведомость отделки (на листе)

Марка	Поверхность	Материал, изделие	Цвет, код	Кол.
О1	стены	окраска, Farrow & Ball Modern Emulsion, матовая, подготовка Q3	Farrow & Ball No. 15 «Bone — мягкий каменно-серый с зеленцой»	7,2 м²
О3	плинтус	плинтус МДФ, h 80 мм, аналог: плинтус МДФ под покраску 80×16	Farrow & Ball No. 15 «Bone — мягкий каменно-серый с зеленцой»	2,8 м
О4	потолок	окраска, Tikkurila Anti-Reflex 2, глубокоматовая, подготовка Q3	Tikkurila V503 «Winter»	18,9 м²

Примечания

1. Размеры — в мм от чистовых поверхностей стен; условные обозначения и общие указания — лист 27.
2. Картины и зеркала крепить к основанию по паспорту изделия (закладные и анкеры — в перечне скрытых работ); крест — ось центра предмета.
3. Двери скрытого монтажа — полотно в плоскости стены, отделка стены по полотну, плинтус прерывается у короба (узел — на листе узлов).
4. Потолок — у каждой стены свой, по плану потолков (ПТ1); ступени — зоной, кромка короба перед нишей — тонкой линией; в поле потолка: ПТ2 +2,600.

	Лист	№ док.	Подпись	Дата
Дизайнер	Кырлан А.С.			04.11.26

Проект: Квартира с кабинетом — **М 1:20**

Развёртка стены В. Кабинет (пом. 3)

Стадия	Лист	Листов
П	84	127

Развёртка стены Г


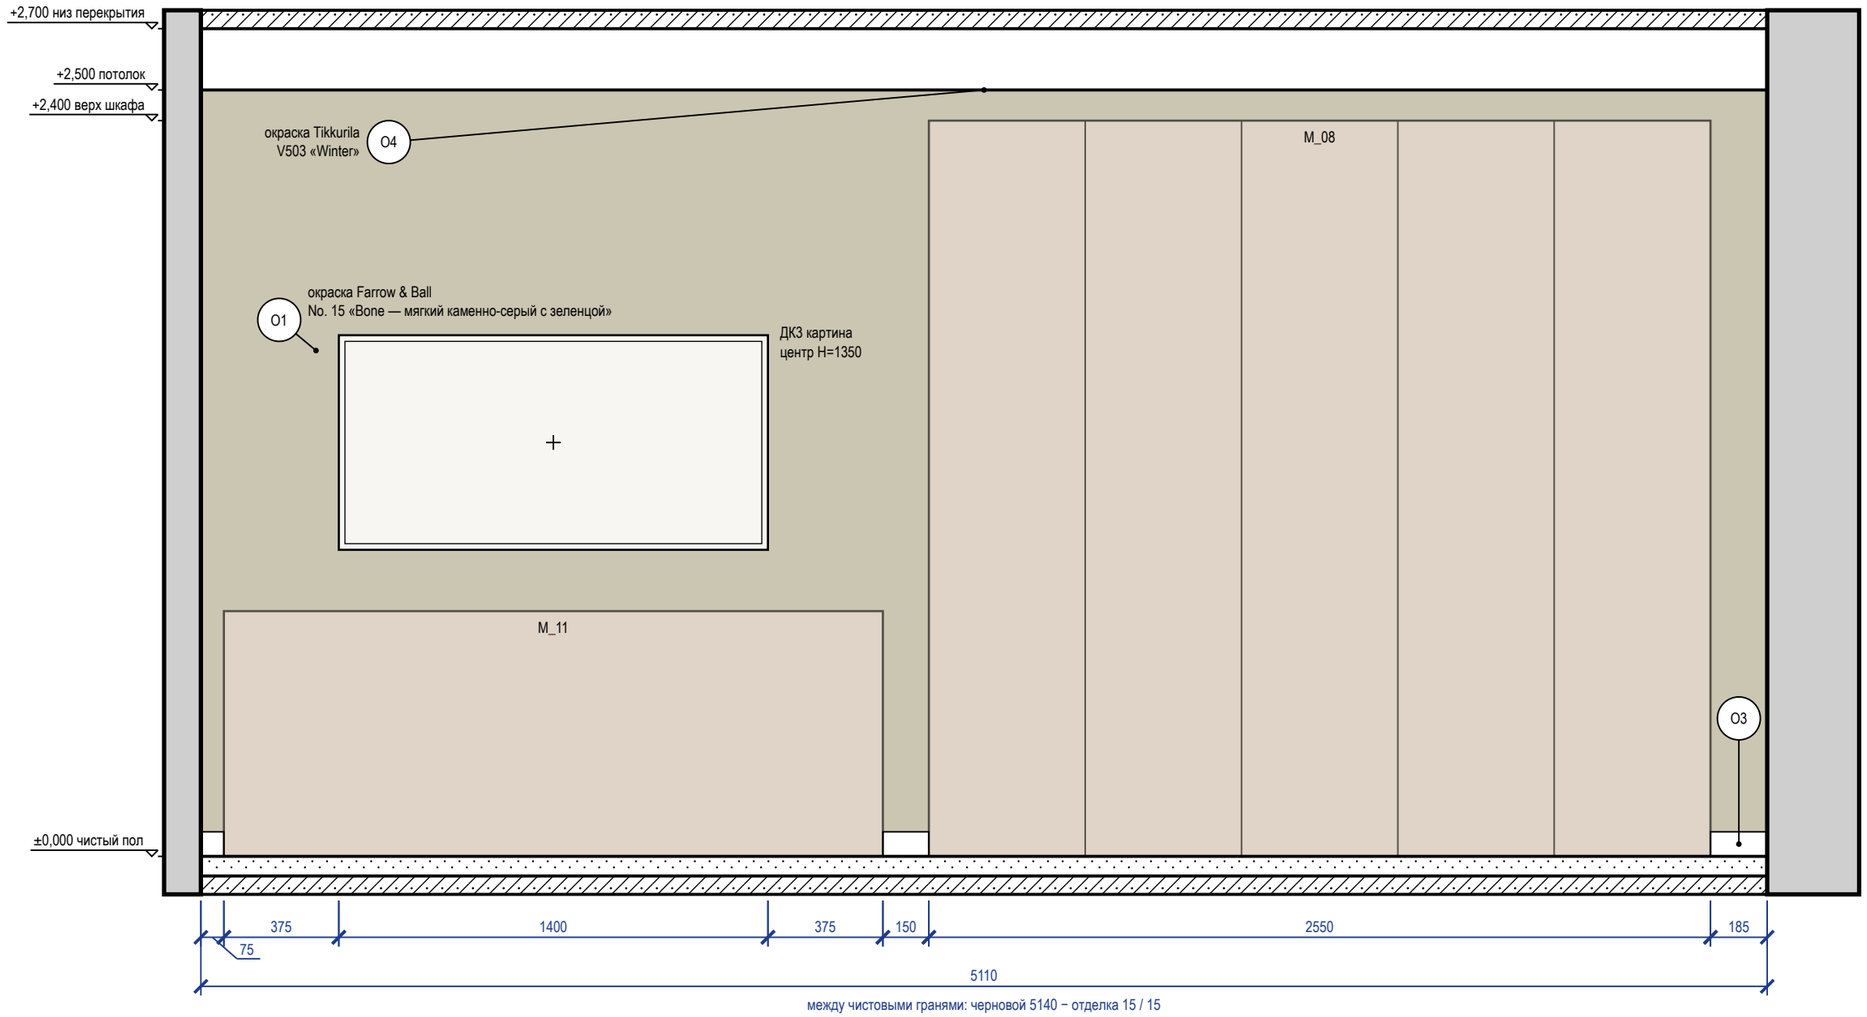



Схема развёрток (М 1:100)

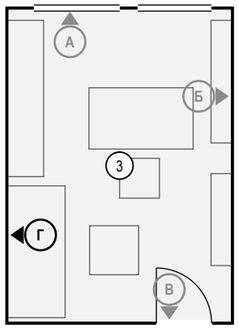

Ведомость отделки (на листе)

Марка	Поверхность	Материал, изделие	Цвет, код	Кол.
O1	стены	окраска, Farrow & Ball Modern Emulsion, матовая, подготовка Q3	Farrow & Ball No. 15 «Bone — мягкий каменно-серый с зеленцой»	12,8 м²
O3	плинтус	плинтус МДФ, h 80 мм, аналог: плинтус МДФ под покраску 80×16	Farrow & Ball No. 15 «Bone — мягкий каменно-серый с зеленцой»	0,4 м
O4	потолок	окраска, Tikkurila Anti-Reflex 2, глубокоматовая, подготовка Q3	Tikkurila V503 «Winter»	18,9 м²

Визуализация этой стены — лист 10

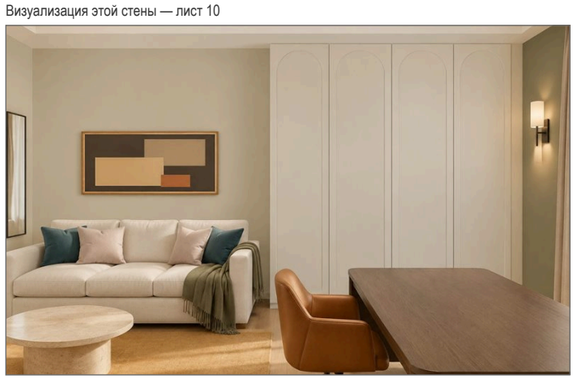

Примечания

1. Размеры — в мм от чистовых поверхностей стен; условные обозначения и общие указания — лист 27.
2. Картины и зеркала крепить к основанию по паспорту изделия (закладные и анкеры — в перечне скрытых работ); крест — ось центра предмета.
3. Потолок — у каждой стены свой, по плану потолков (ПТ1); ступени — зоной, кромка короба перед нишей — тонкой линией; в поле потолка: ПТ2 +2,600.

					Проект: Квартира с кабинетом	М 1:20
	Лист	№ док.	Подпись	Дата	Развёртка стены Г. Кабинет (пом. 3)	Стадия: П; Лист: 85; Листов: 127
Дизайнер	Кырлан А.С.			04.11.26		

выпуск 04.11.2026 № 627e1ac6ce · стр. 85 из 127

Развёртка стены Г


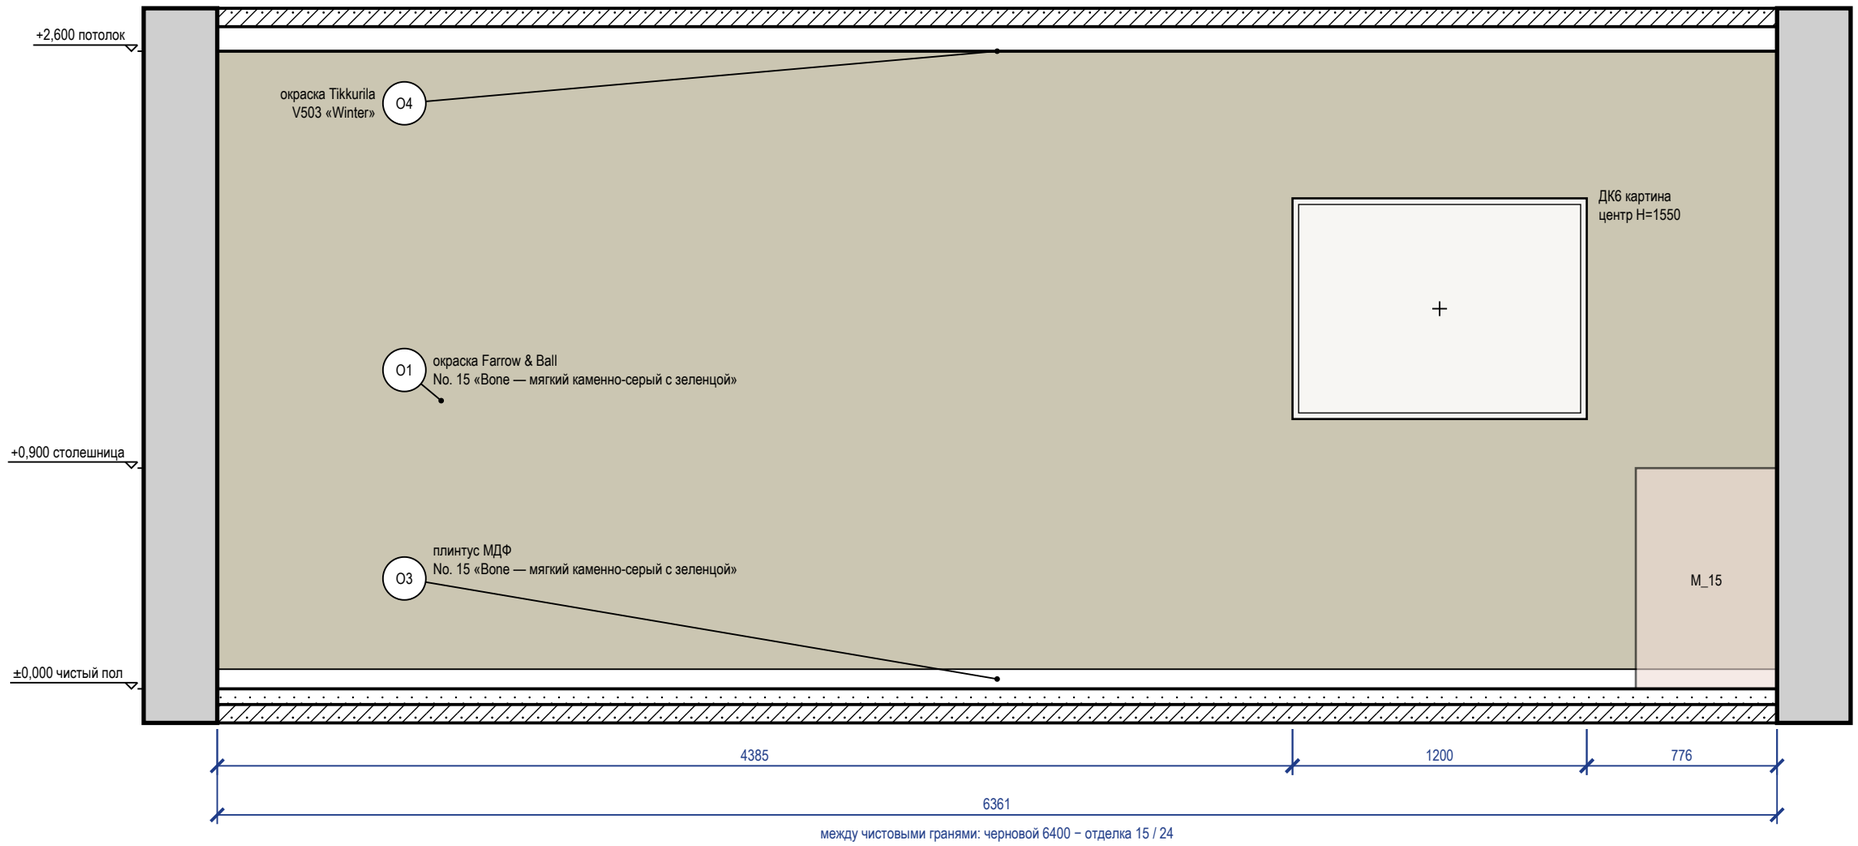


Схема развёрток (М 1:100)

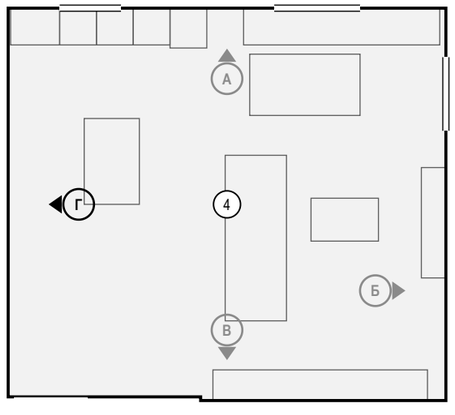

Ведомость отделки (на листе)

Марка	Поверхность	Материал, изделие	Цвет, код	Кол.
O1	стены	окраска, Farrow & Ball Modern Emulsion, матовая, подготовка Q3	Farrow & Ball No. 15 «Bone — мягкий каменно-серый с зеленцой»	16,5 м²
O3	плинтус	плинтус МДФ, h 80 мм, аналог: плинтус МДФ под покраску 80×16	Farrow & Ball No. 15 «Bone — мягкий каменно-серый с зеленцой»	6,4 м
O4	потолок	окраска, Tikkurila Anti-Reflex 2, глубокоматовая, подготовка Q3	Tikkurila V503 «Winter»	45,5 м²

Визуализация этой стены — лист 14



Примечания

1. Размеры — в мм от чистовых поверхностей стен; условные обозначения и общие указания — лист 27.
2. Стена Г показана двумя видами: здесь — архитектурная развёртка (мебель, отделка, проёмы, высоты), электроточки и выводы ВК с привязками и таблицей — на листе 87 («Привязки»).
3. Картины и зеркала крепить к основанию по паспорту изделия (закладные и анкеры — в перечне скрытых работ); крест — ось центра предмета.
4. Потолок — у каждой стены свой, по плану потолков (ПТ2); ступени — зоной, кромка короба перед нишей — тонкой линией; в поле потолка: ПТ1 +2,500.

					Проект: Квартира с кабинетом		М 1:25
	Лист	№ док.	Подпись	Дата			
Дизайнер	Кырлан А.С.			04.11.26	Развёртка стены Г. Кухня-гостиная (пом. 4), кухонный фронт	Стадия	Лист	Листов
						П	86	127

Развёртка стены Г: электроточки и выводы

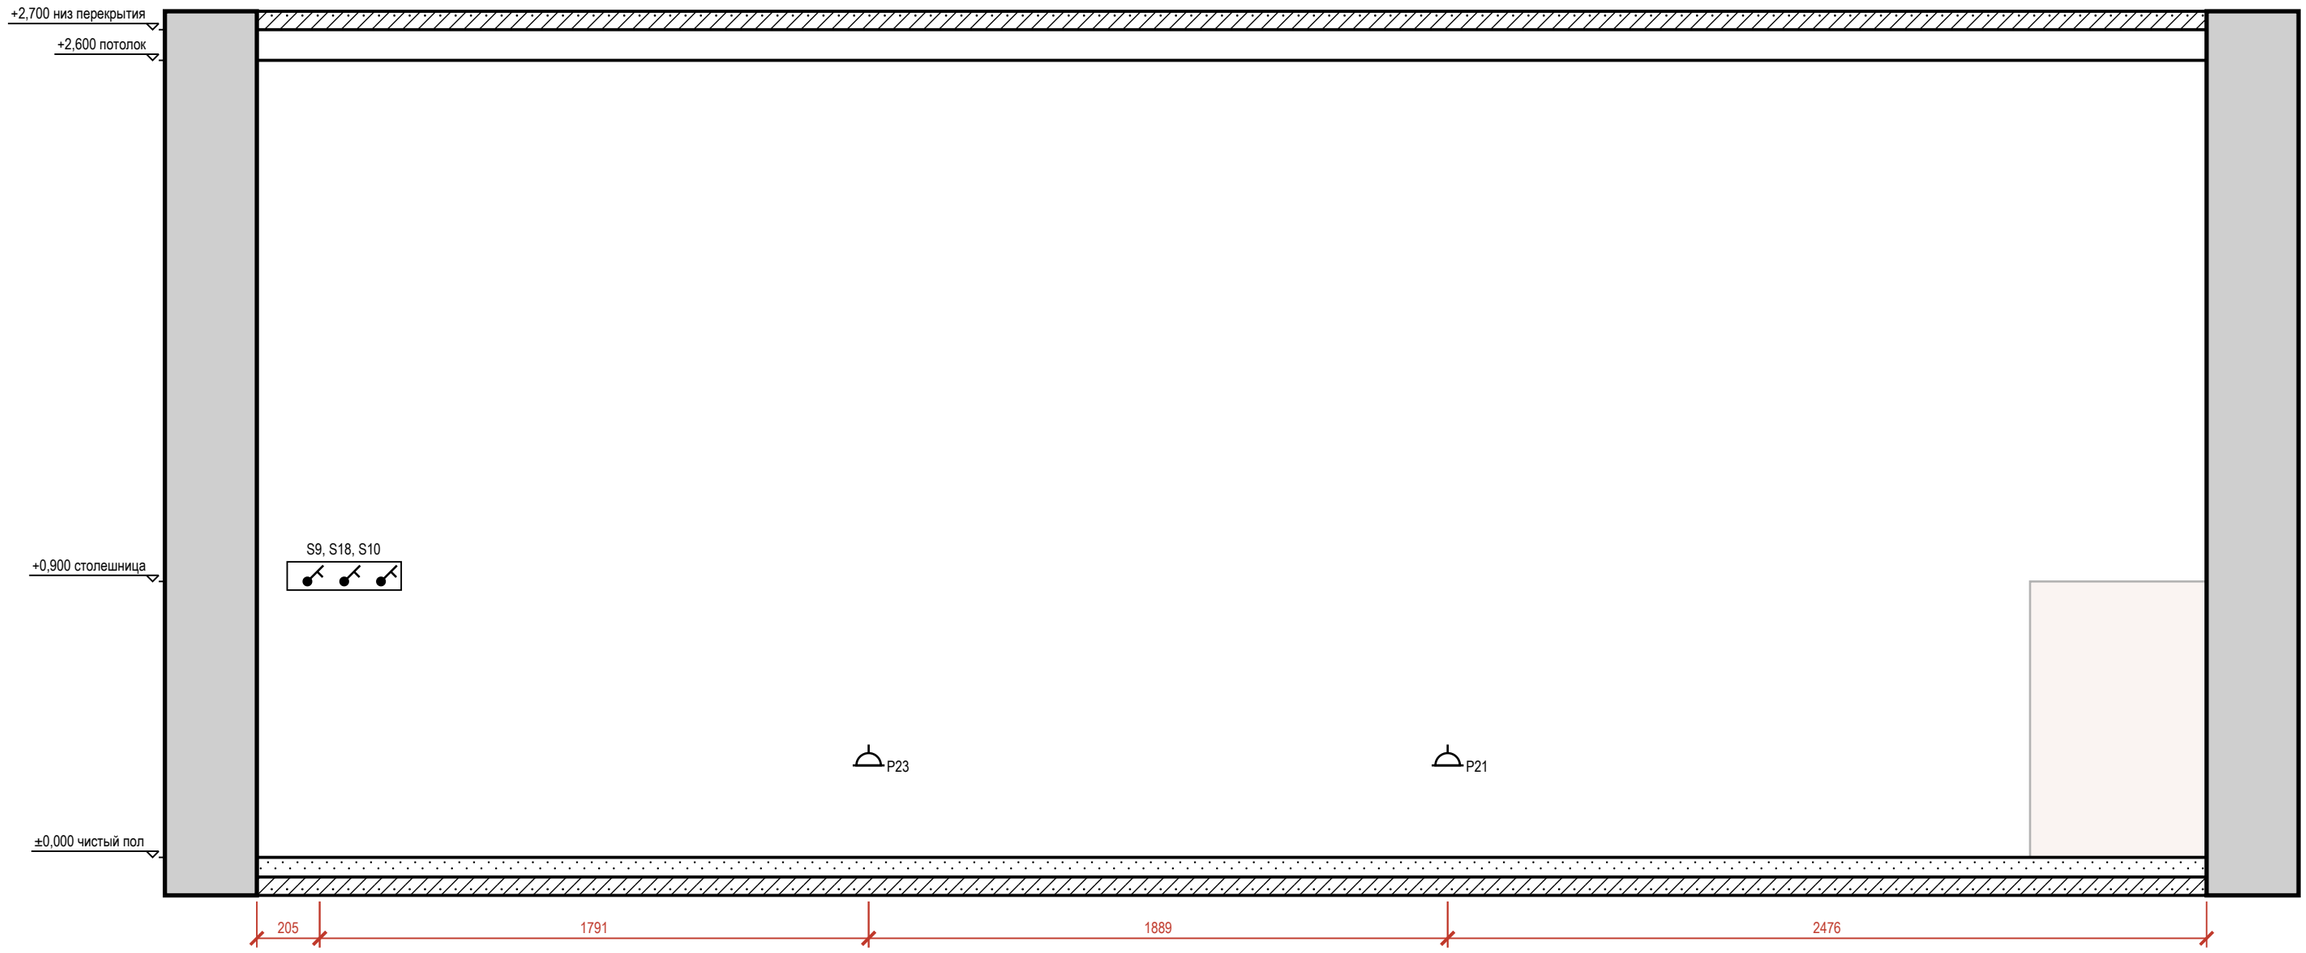



Таблица привязок электроточек и выводов

Марка	Назначение	От угла, мм	H от пола, мм	Примечание
S9	выключатель	205	900	гр. 2
S18	выключатель	285	900	гр. 2
S10	выключатель	365	900	гр. 2
P23	розетка: уборка, пылесос	1996	300	гр. 6
P21	розетка: общего назначения	3885	300	гр. 6

Условные обозначения

- розетка с заземляющим контактом; у знака — марка, ×N постов в рамке, гр. — группа щита, H — высота оси, мм
- выключатель одноклавишный
- привязки точек и выводов от угла и от пола, мм
- А — марка развёртки: буква стены, стрелка — взгляд

Схема развёрток (М 1:200)

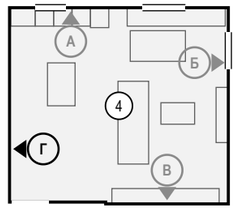

Примечания

1. Вид «Привязки» стены Г — электроточки и выводы ВК; архитектурная развёртка (мебель, отделка, проёмы, высоты) — на листе 86. Мебель и приборы — подложкой для ориентира; их марки и обозначения мебели, проёмов и стен — там же.
2. Привязки — в мм: по горизонтали от левого чистового угла стены до оси изделия, H — от чистого пола до оси; все точки — в таблице привязок. Красная цепочка — привязки по осям; точки ближе 120 мм одна к другой в цепочку не дробятся — их привязки только в таблице.
3. У знака — марка электроточки (Р — розетка, S — выключатель, Св — светильник, ЭВ — вывод кабеля); условные обозначения и общие указания — лист 27.
4. Выводы кухонной техники — по утверждённому проекту кухни: привязки выводов даются от осей модулей гарнитура.

					Проект: Квартира с кабинетом — М 1:20
	Лист	№ док.	Подпись	Дата	
Дизайнер	Кырлан А.С.			04.11.26	Привязки электроточек, стена Г. Кухня-гостиная (пом. 4)

Стадия	Лист	Листов
П	87	127

Развёртка стены А


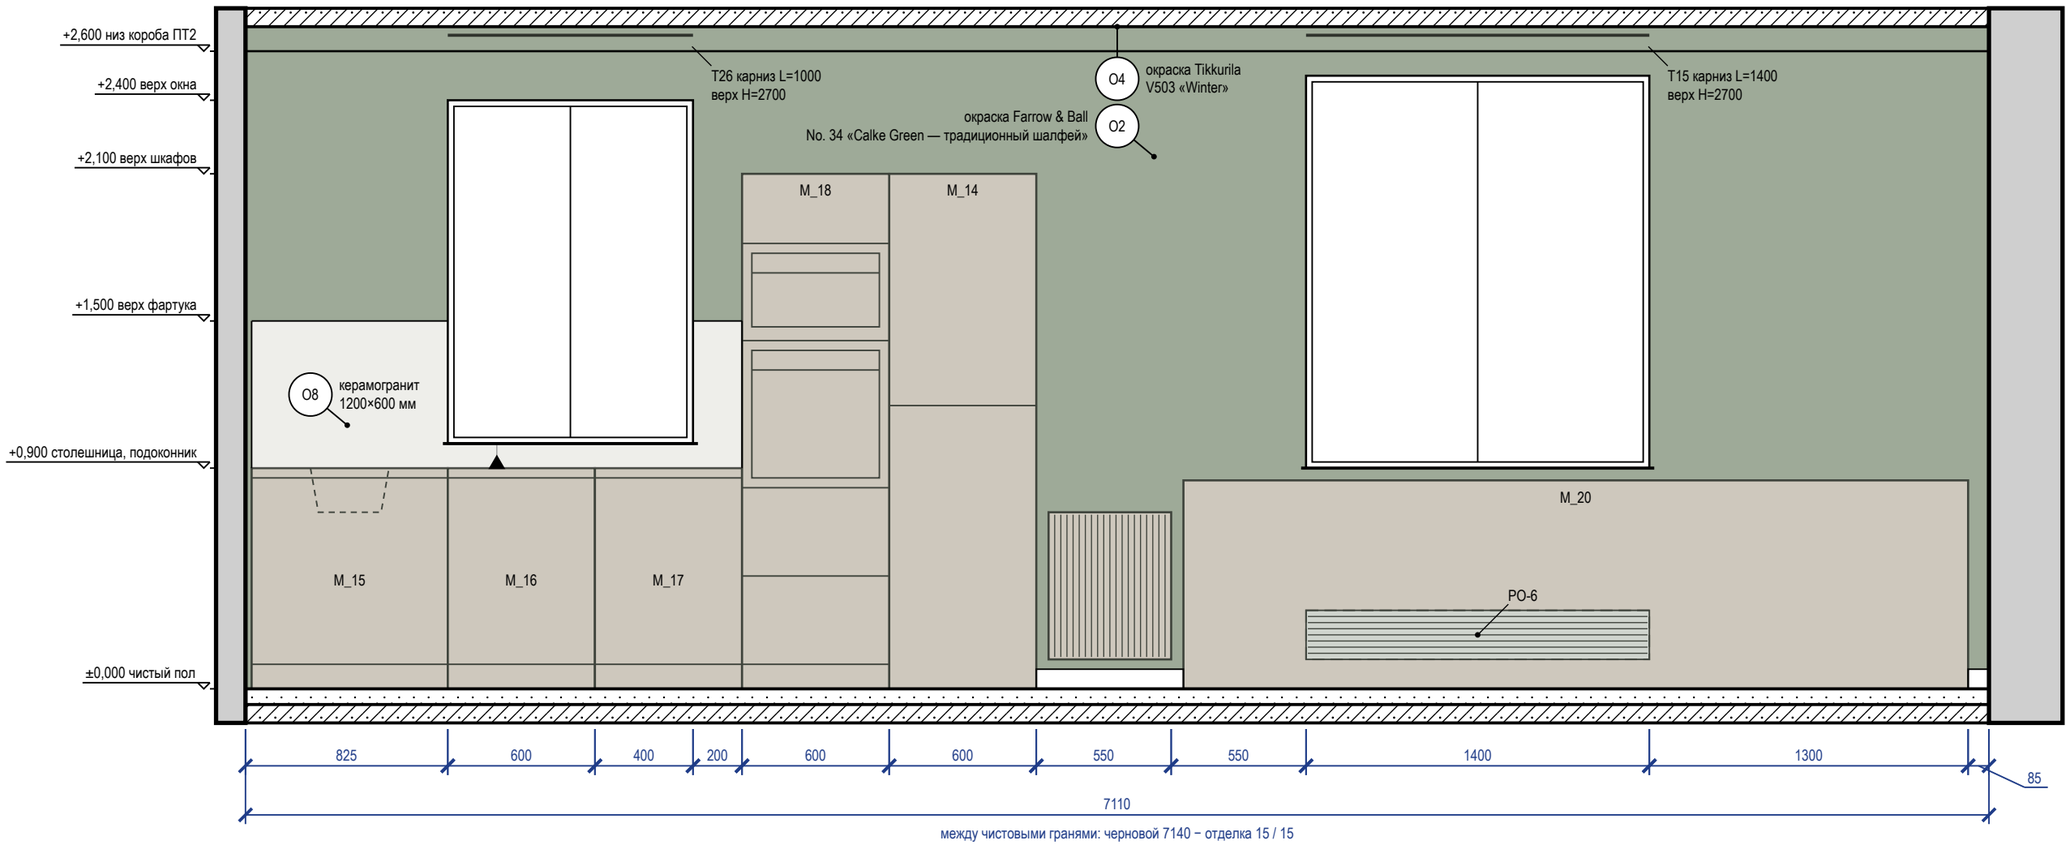



Схема развёрток (М 1:100)

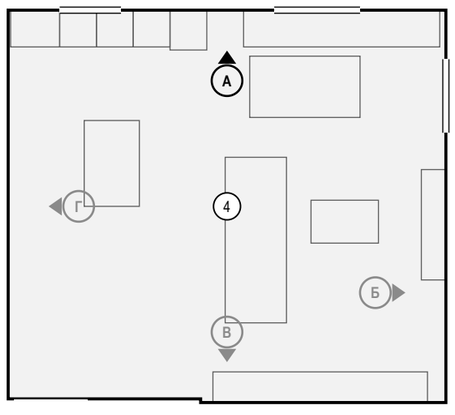

Ведомость отделки (на листе)

Марка	Поверхность	Материал, изделие	Цвет, код	Кол.
О2	акцентная стена	окраска, Farrow & Ball Modern Emulsion, матовая, подготовка Q3	Farrow & Ball No. 34 «Calke Green традиционный шалфей»	14,4 м²
О3	плинтус	плинтус МДФ, h 80 мм, аналог: плинтус МДФ под покраску 80×16	Farrow & Ball No. 15 «Bone — мягкий каменно-серый с зеленцой»	0,7 м
О4	потолок	окраска, Tikkurila Anti-Reflex 2, глубокоматовая, подготовка Q3	Tikkurila V503 «Winter»	45,5 м²
О8	фартук	керамогранит, 1200×600×9 мм, аналог: керамогранит под травертин, матовый, затирка CG2WA		0,7 м²

Визуализация этой стены — лист 11

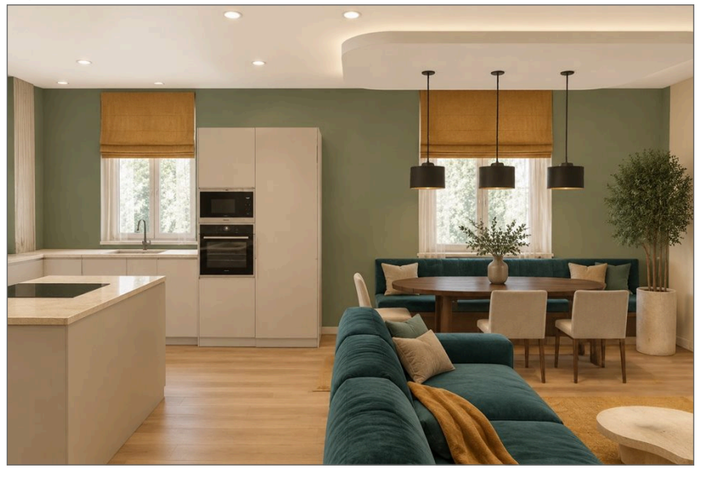

Примечания

1. Размеры — в мм от чистовых поверхностей стен; условные обозначения и общие указания — лист 27.
2. Стена А показана двумя видами: здесь — архитектурная развёртка (мебель, отделка, проёмы, высоты), электроточки и выводы ВК с привязками и таблицей — на листе 89 («Привязки»).
3. Радиатор за корпусом мебели — штриховой линией; горизонтальные ламели — решётка экрана в лицевой панели по ширине прибора, щель для тёплого воздуха над прибором — по чертежу изделия.
4. Карнизы (шины) — по ведомости текстиля декоратора: длина L и верх H на развёртке — те же числа, что в ведомости; крепление — до окраски потолка.
5. Высота фартука принята 600 мм над столешницей там, где нет навесных модулей и высота фартука не задана.
6. Потолок — у каждой стены свой, по плану потолков (НШ2, ПТ2); ступени — зоной, кромка короба перед нишей — тонкой линией; в поле потолка: ПТ1 +2,500.

					Проект: Квартира с кабинетом — М 1:25
	Лист	№ док.	Подпись	Дата	Развёртка стены А. Кухня-гостиная (пом. 4), кухонный фронт
Дизайнер	Кырлан А.С.			04.11.26	Стадия: П; Лист: 88; Листов: 127

Развёртка стены А: электроточки и выводы

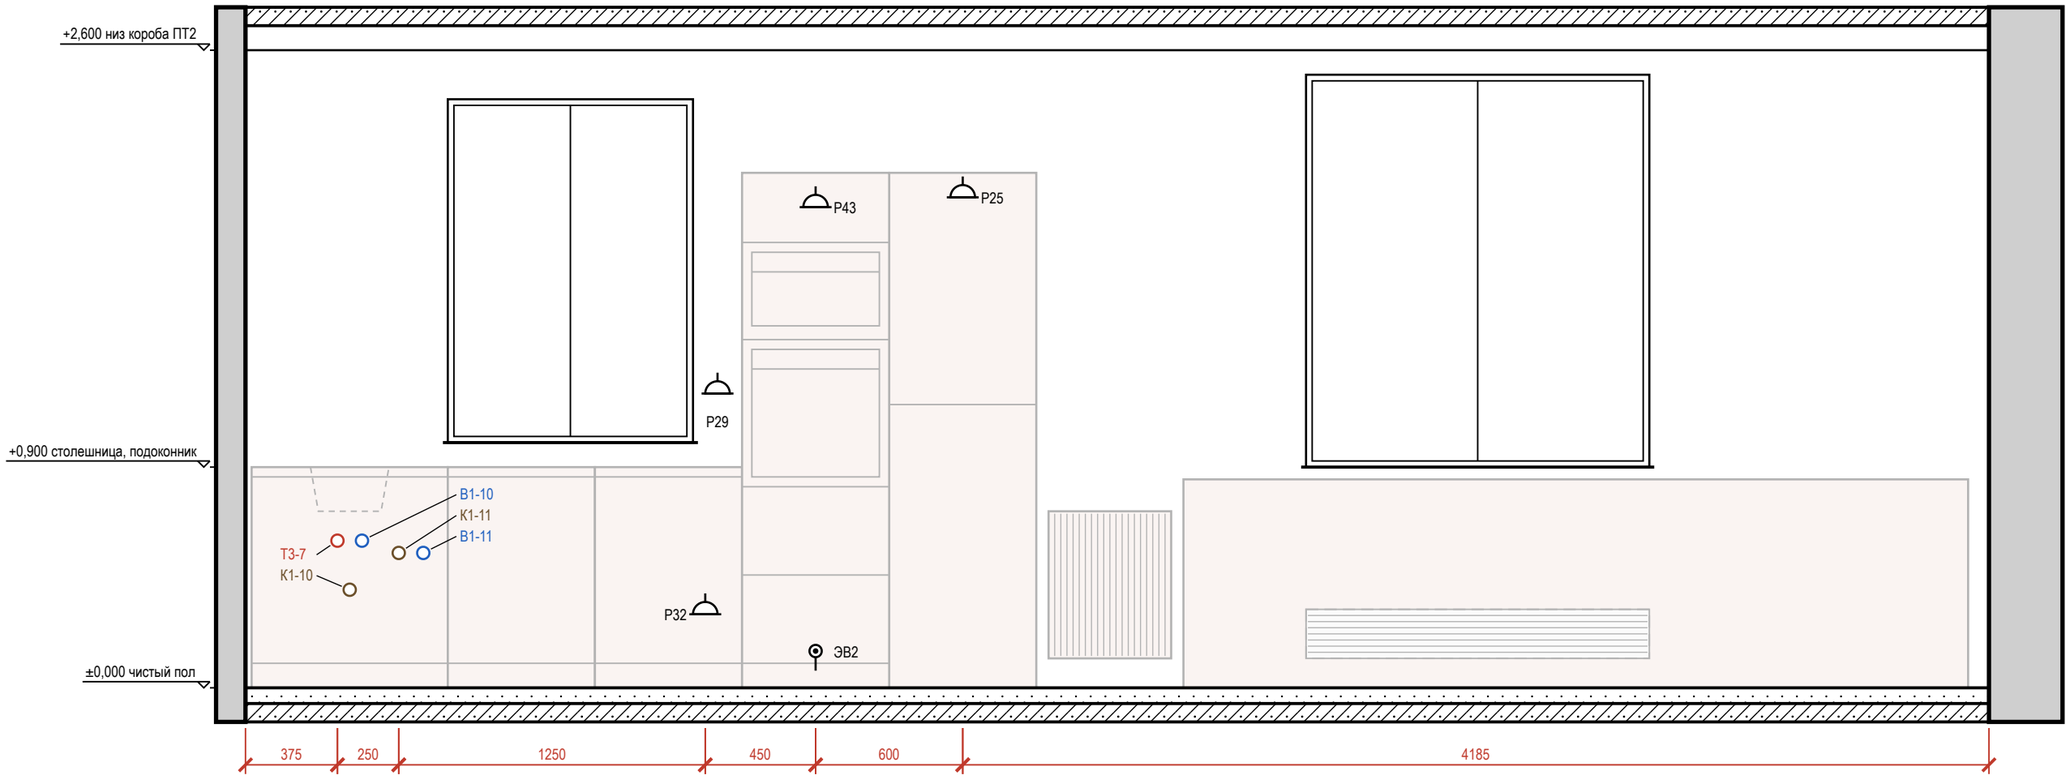



Таблица привязок электроточек и выводов

Марка	Назначение	От угла, мм	Н от пола, мм	Примечание
Т3-7	горячая вода — мойка кухонная	375	600	межос. 100
К1-10	канализация — мойка кухонная	425	400	Ø50
В1-10	холодная вода — мойка кухонная	475	600	межос. 100
К1-11	канализация — посудомоечная машина	625	550	Ø40; слив ПММ в шкафу мойки
В1-11	холодная вода — посудомоечная машина	725	550	кран ПММ в шкафу мойки
Р32	розетка: посудомоечная машина — в соседнем модуле, за ящиком	1875	300	гр. 10
Р29	розетка: фартук	1925	1200	гр. 7
ЭВ2	вывод кабеля: духовой шкаф — в цоколе	2325	150	гр. 9
Р43	розетка: СВЧ — над нишей, съёмная панель	2325	1960	гр. 7
Р25	розетка: холодильник — над нишей, съёмная панель	2925	2000	гр. 11

Условные обозначения

- розетка с заземляющим контактом; у знака — марка, ×N постов в рамке, гр. — группа щита, Н — высота оси, мм
- вывод кабеля для подключения прибора (без розетки), марка ЭВ
- вывод В1 (код — в ведомости привязок)
- вывод Т3 (код — в ведомости привязок)
- вывод К1 (код — в ведомости привязок)
- привязки точек и выводов от угла и от пола, мм
- марка развёртки: буква стены, стрелка — взгляд

Схема развёрток (М 1:200)

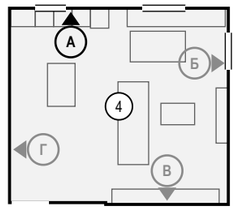

Примечания

1. Вид «Привязки» стены А — электроточки и выводы ВК; архитектурная развёртка (мебель, отделка, проёмы, высоты) — на листе 88. Мебель и приборы — подложкой для ориентира; их марки и обозначения мебели, проёмов и стен — там же.
2. Привязки — в мм: по горизонтали от левого чистового угла стены до оси изделия, Н — от чистого пола до оси; все точки — в таблице привязок. Красная цепочка — привязки по осям; точки ближе 150 мм одна к другой в цепочку не дробятся — их привязки только в таблице.
3. У знака — марка электроточки (Р — розетка, S — выключатель, Св — светильник, ЭВ — вывод кабеля); условные обозначения и общие указания — лист 27.
4. Коды выводов ВК: В1 — холодная вода, Т3 — горячая вода, К1 — канализация; номер после дефиса — номер вывода на листе выводов сантехники.
5. Выводы кухонной техники — по утверждённому проекту кухни: привязки выводов даются от осей модулей гарнитура.

					Проект: Квартира с кабинетом	М 1:25
	Лист	№ док.	Подпись	Дата	Привязки электроточек и выводов ВК, стена А. Кухня-гостиная (пом. 4)	Стадия / Лист / Листов
Дизайнер	Кырлан А.С.			04.11.26		П / 89 / 127

Развёртка стены Б


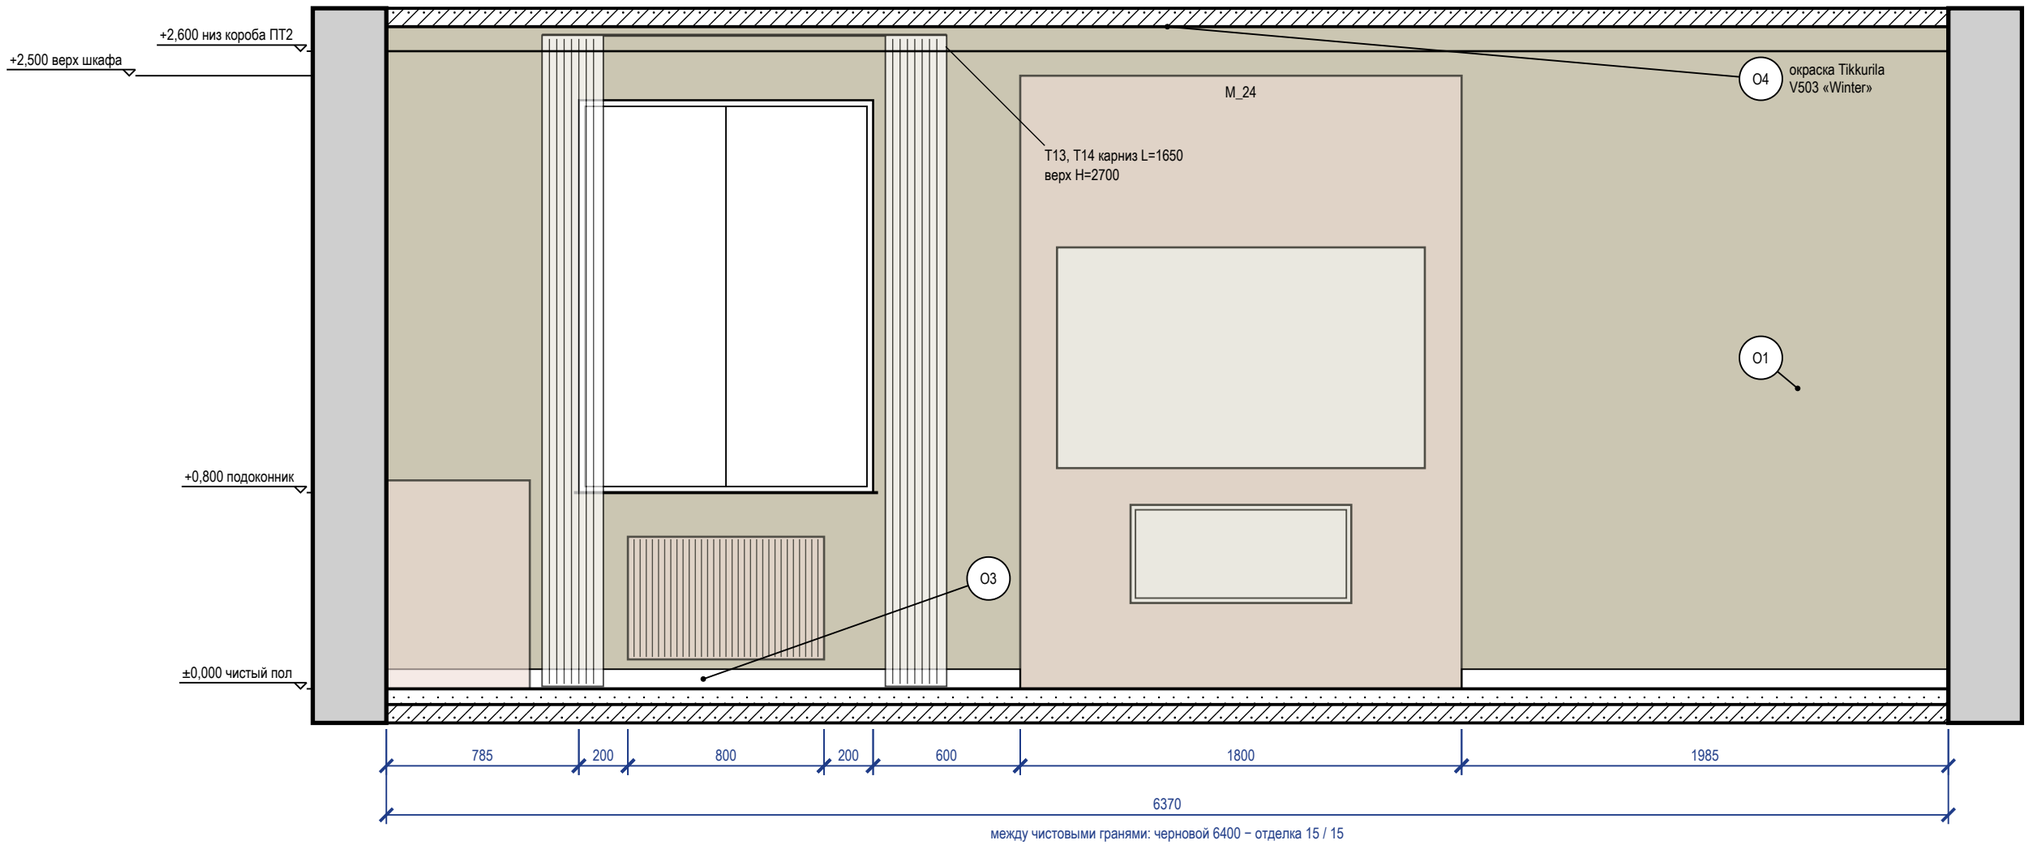



Схема развёрток (М 1:100)

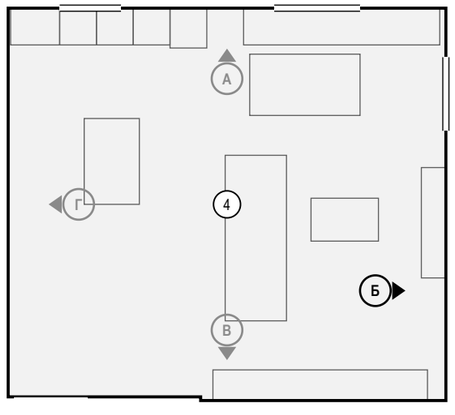

Ведомость отделки (на листе)

Марка	Поверхность	Материал, изделие	Цвет, код	Кол.
O1	стены	окраска, Farrow & Ball Modern Emulsion, матовая, подготовка Q3	Farrow & Ball No. 15 «Bone — мягкий каменно-серый с зеленцой»	15,3 м²
O3	плинтус	плинтус МДФ, h 80 мм, аналог: плинтус МДФ под покраску 80×16	Farrow & Ball No. 15 «Bone — мягкий каменно-серый с зеленцой»	4,6 м
O4	потолок	окраска, Tikkurila Anti-Reflex 2, глубокоматовая, подготовка Q3	Tikkurila V503 «Winter»	45,5 м²

Визуализация этой стены — лист 12

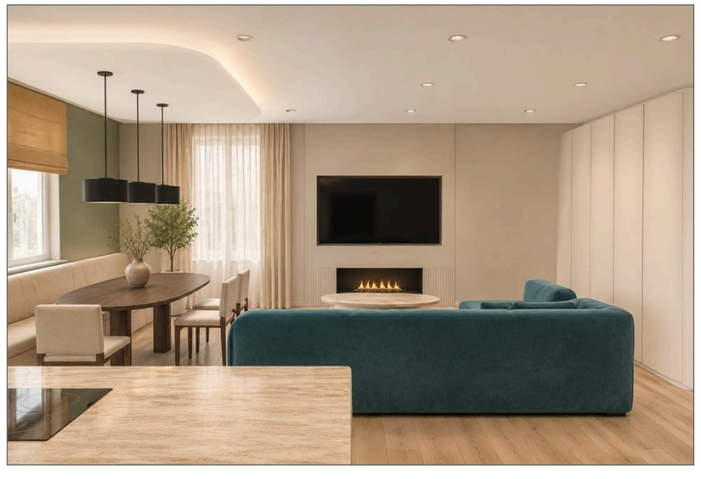

Примечания

1. Размеры — в мм от чистовых поверхностей стен; условные обозначения и общие указания — лист 27.
2. Стена Б показана двумя видами: здесь — архитектурная развёртка (мебель, отделка, проёмы, высоты), электроточки и выводы ВК с привязками и таблицей — на листе 91 («Привязки»).
3. Карнизы (шины) — по ведомости текстиля декоратора: длина L и верх H на развёртке — те же числа, что в ведомости; крепление — до окраски потолка.
4. Потолок — у каждой стены свой, по плану потолков (НШ2, ПТ2); ступени — зоной, кромка короба перед нишей — тонкой линией; в поле потолка: ПТ1 +2,500.

					Проект: Квартира с кабинетом	М 1:25
	Лист	№ док.	Подпись	Дата		
Дизайнер	Кырлан А.С.			04.11.26	Развёртка стены Б. Кухня-гостиная (пом. 4)	Стадия: П; Лист: 90; Листов: 127

Развёртка стены Б: электроточки и выводы

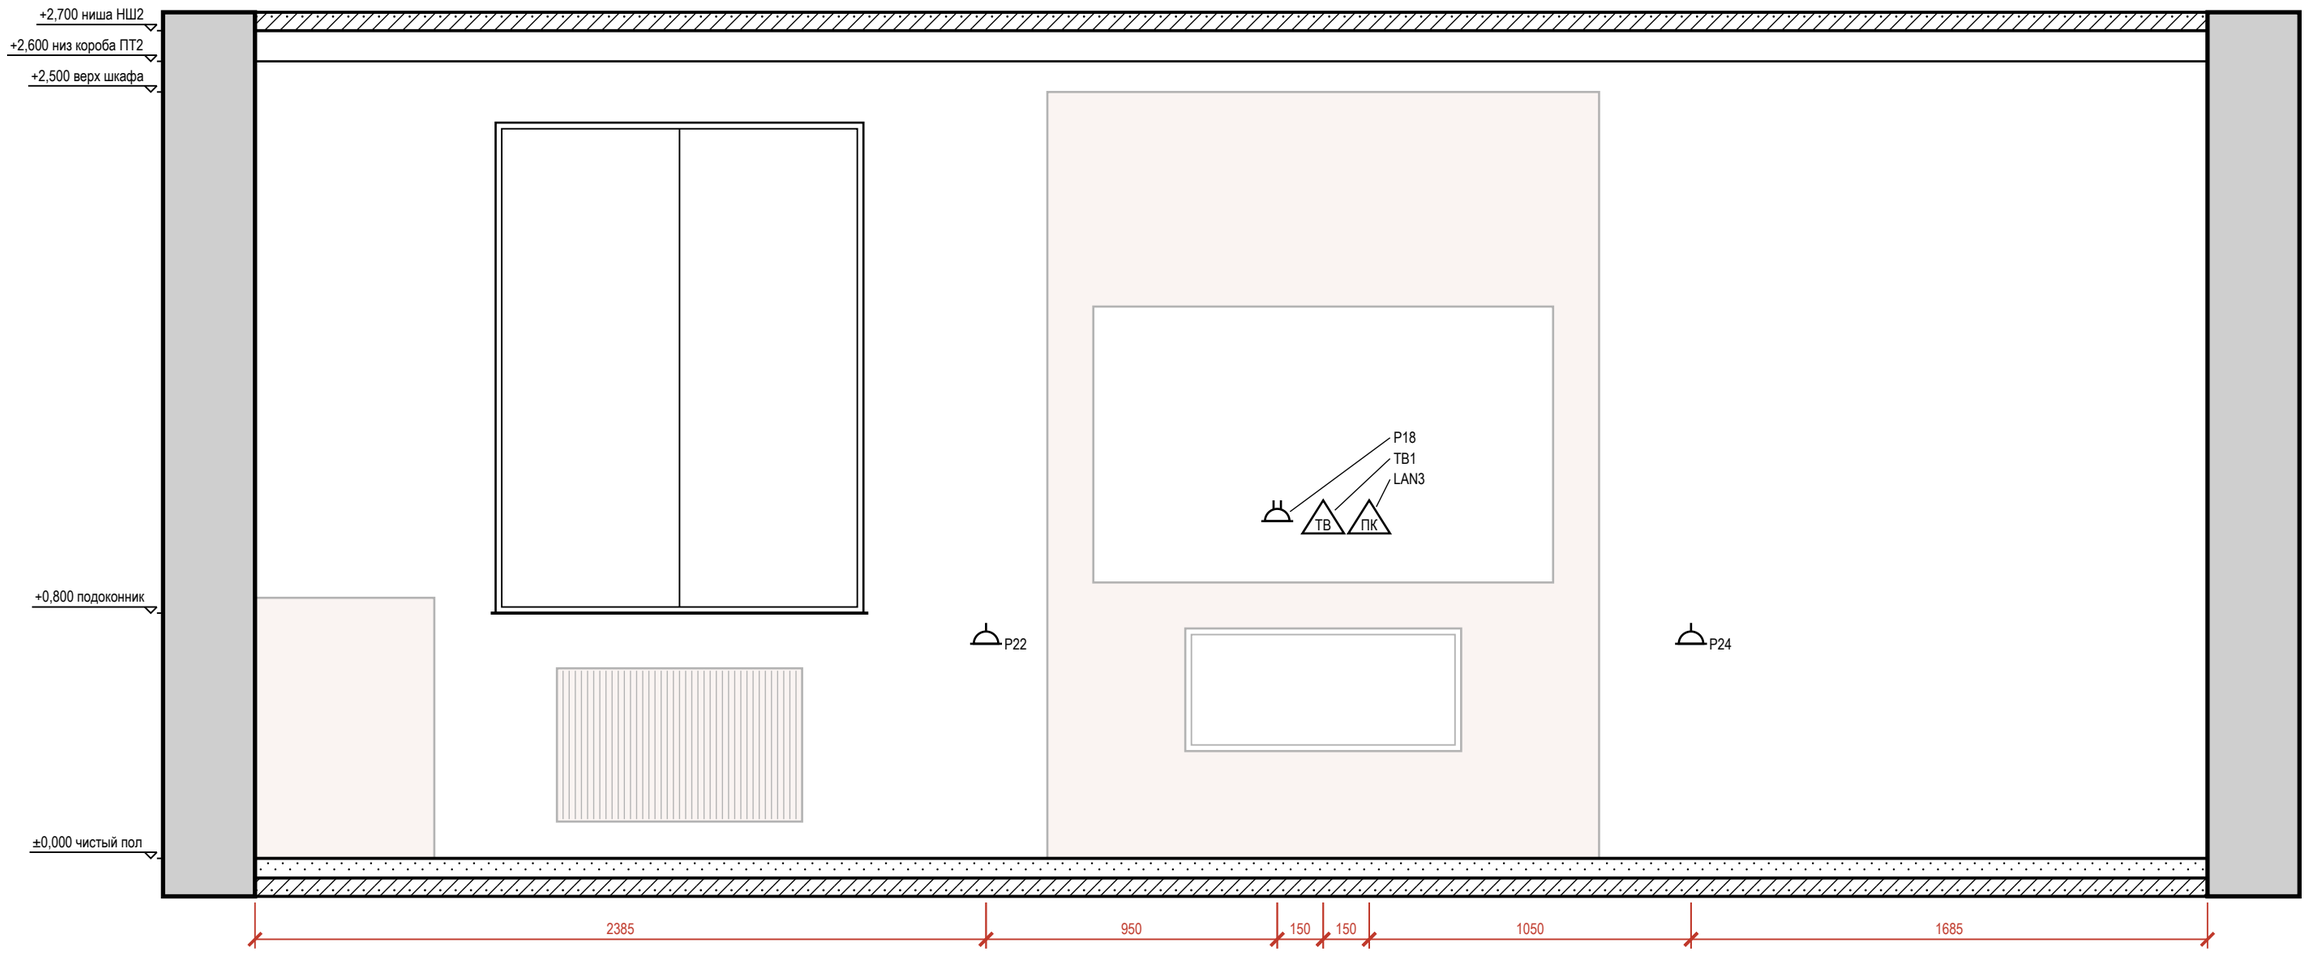



Таблица привязок электроточек и выводов

Марка	Назначение	От угла, мм	Н от пола, мм	Примечание
P22	розетка: общего назначения	2385	700	гр. 6
P18	розетка: ТВ-зона: питание ТВ и приставки	3335	1100	рамка 2 поста, гр. 6
TB1	розетка ТВ: ТВ-зона	3485	1100	
LAN3	розетка RJ45: ТВ-зона: Smart TV	3635	1100	
P24	розетка: общего назначения	4685	700	гр. 6

Условные обозначения

- розетка с заземляющим контактом; у знака — марка, ×N постов в рамке, гр. — группа щита, Н — высота оси, мм
- ПК — розетка компьютерная RJ45
- ТВ — розетка телевизионная
- привязки точек и выводов от угла и от пола, мм
- А — марка развёртки: буква стены, стрелка — взгляд

Схема развёрток (М 1:200)

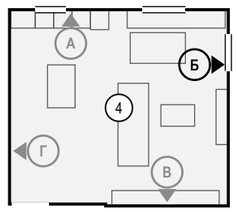

Примечания

1. Вид «Привязки» стены Б — электроточки и выводы ВК; архитектурная развёртка (мебель, отделка, проёмы, высоты) — на листе 90. Мебель и приборы — подложкой для ориентира; их марки и обозначения мебели, проёмов и стен — там же.
2. Привязки — в мм: по горизонтали от левого чистового угла стены до оси изделия, Н — от чистого пола до оси; все точки — в таблице привязок. Красная цепочка — привязки по осям; точки ближе 120 мм одна к другой в цепочку не дробятся — их привязки только в таблице.
3. У знака — марка электроточки (Р — розетка, S — выключатель, Св — светильник, ЭВ — вывод кабеля); условные обозначения и общие указания — лист 27.

					Проект: Квартира с кабинетом — М 1:20
	Лист	№ док.	Подпись	Дата	
Дизайнер	Кырлан А.С.			04.11.26	Привязки электроточек, стена Б. Кухня-гостиная (пом. 4)
					Стадия: П; Лист: 91; Листов: 127

выпуск 04.11.2026 № 627e1ac6ce · стр. 91 из 127

Развёртка стены В


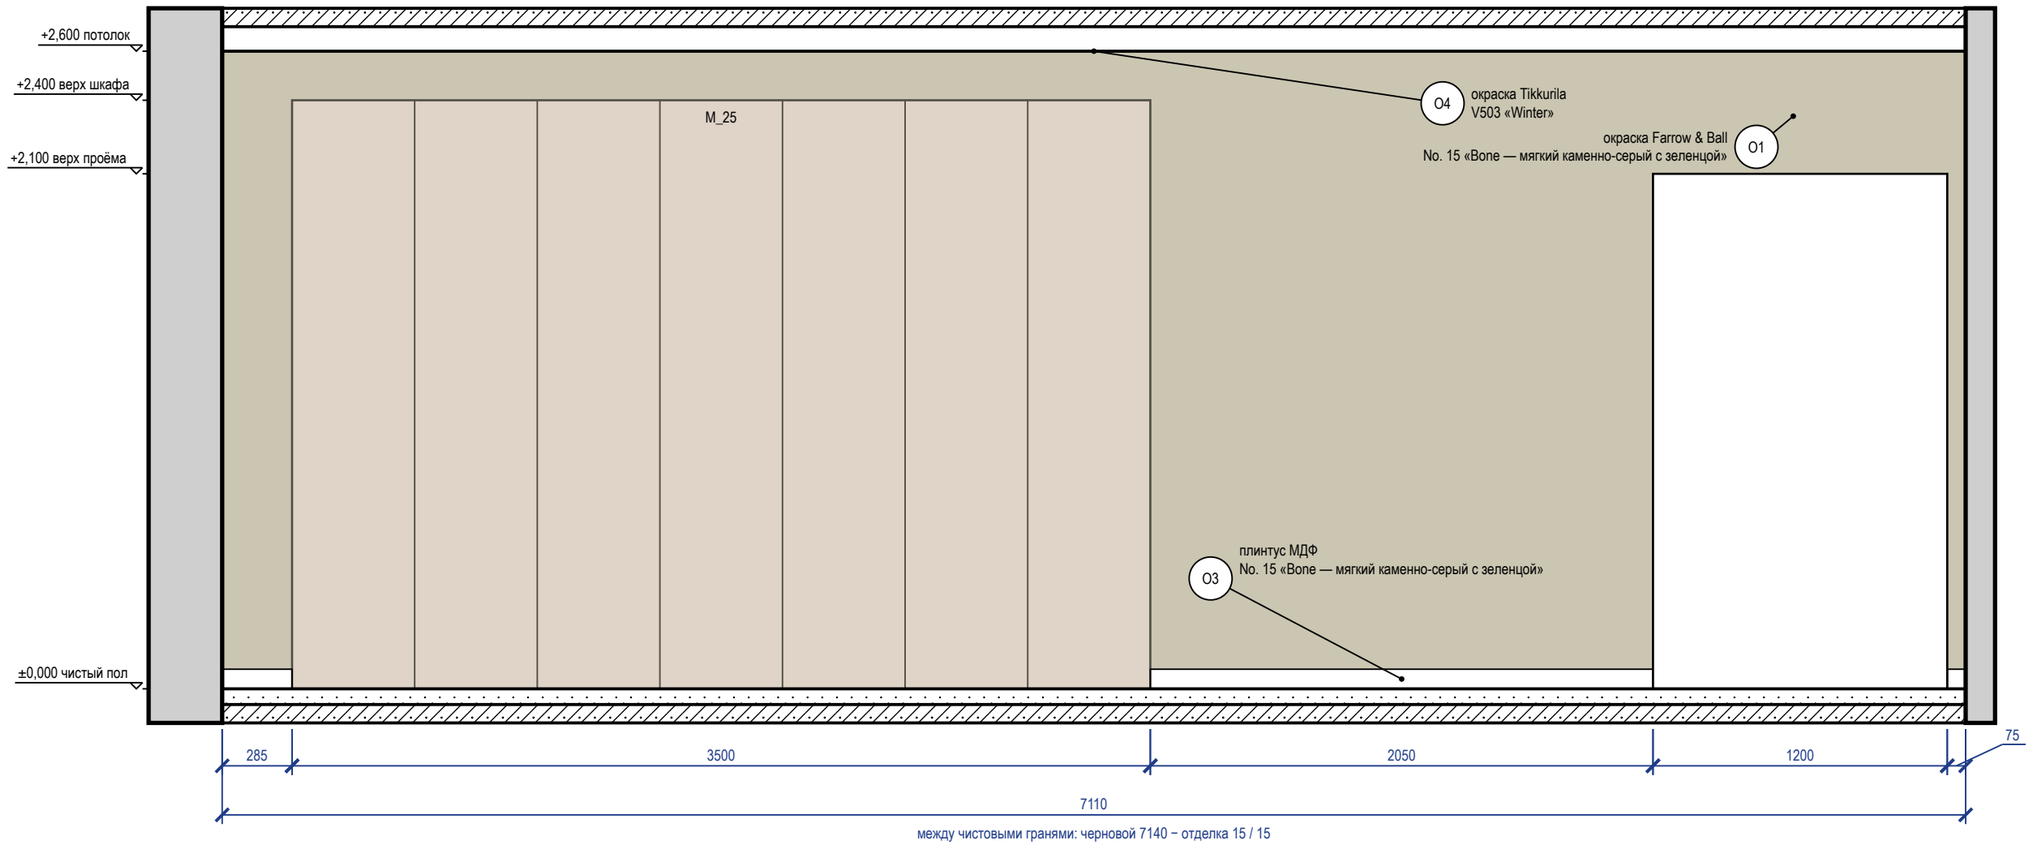



Схема развёрток (М 1:100)

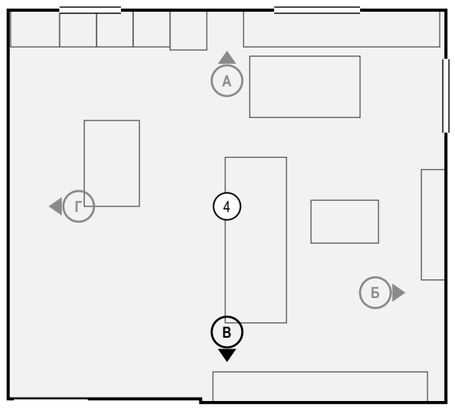

Ведомость отделки (на листе)

Марка	Поверхность	Материал, изделие	Цвет, код	Кол.
O1	стены	окраска, Farrow & Ball Modern Emulsion, матовая, подготовка Q3	Farrow & Ball No. 15 «Bone — мягкий каменно-серый с зеленцой»	16 м²
O3	плинтус	плинтус МДФ, h 80 мм, аналог: плинтус МДФ под покраску 80×16	Farrow & Ball No. 15 «Bone — мягкий каменно-серый с зеленцой»	2,4 м
O4	потолок	окраска, Tikkurila Anti-Reflex 2, глубокоматовая, подготовка Q3	Tikkurila V503 «Winter»	45,5 м²

Визуализация этой стены — лист 13

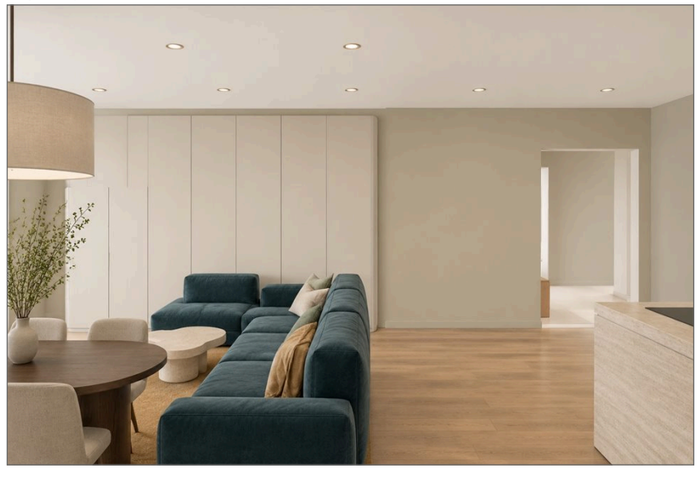


Примечания

1. Размеры — в мм от чистовых поверхностей стен; условные обозначения и общие указания — лист 27.
2. Потолок — у каждой стены свой, по плану потолков (ПТ2); ступени — зоной, кромка короба перед нишей — тонкой линией; в поле потолка: ПТ1 +2,500.


					Проект: Квартира с кабинетом	М 1:25
	Лист	№ док.	Подпись	Дата	Развёртка стены В. Кухня-гостиная (пом. 4)	Стадия / Лист / Листов
Дизайнер	Кырлан А.С.			04.11.26		П / 92 / 127

Развёртка стены А1

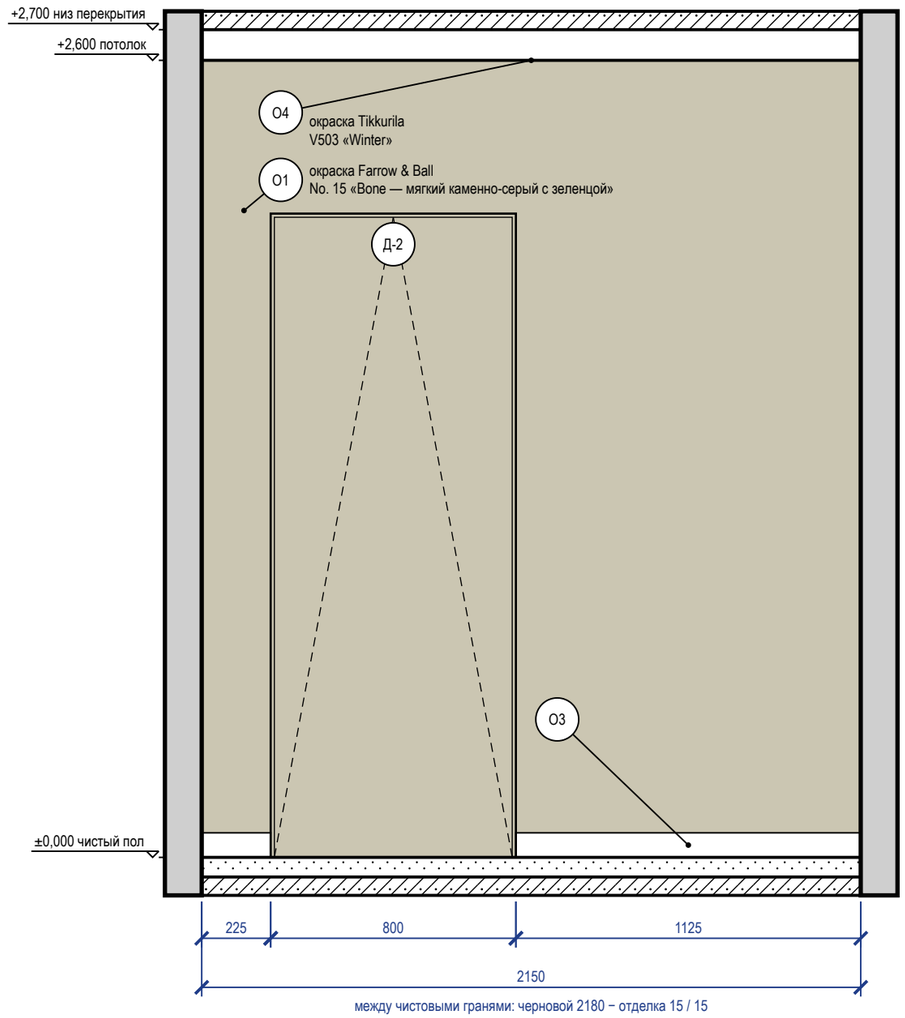


между чистовыми гранями: черновой 2180 − отделка 15 / 15

Развёртка стены Г

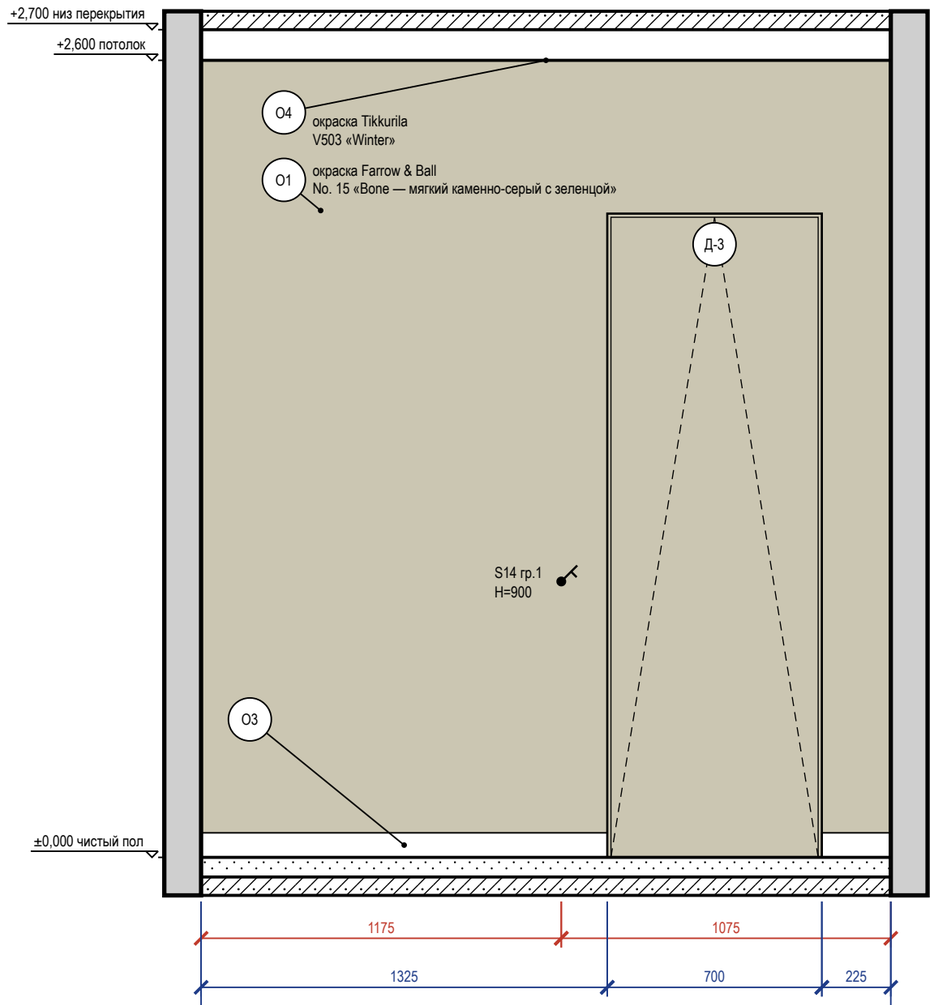

между чистовыми гранями: черновой 2280 − отделка 15 / 15

Схема развёрток (М 1:100)

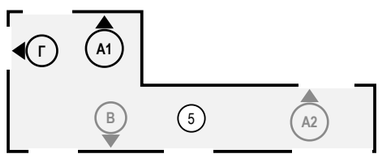

Ведомость отделки (на листе)

Марка	Поверхность	Материал, изделие	Цвет, код	Кол.
О1	стены	окраска, Farrow & Ball Modern Emulsion, матовая, подготовка Q3	Farrow & Ball No. 15 «Bone — мягкий каменно-серый с зеленцой»	8,3 м²
О3	плинтус	плинтус МДФ, h 80 мм, аналог: плинтус МДФ под покраску 80×16	Farrow & Ball No. 15 «Bone — мягкий каменно-серый с зеленцой»	2,9 м
О4	потолок	окраска, Tikkurila Anti-Reflex 2, глубокоматовая, подготовка Q3	Tikkurila V503 «Winter»	9,1 м²

Примечания

1. Размеры — в мм от чистовых поверхностей стен; условные обозначения и общие указания — лист 27.
2. Двери скрытого монтажа — полотно в плоскости стены, отделка стены по полотну, плинтус прерывается у короба (узел — на листе узлов).

	Лист	№ док.	Подпись	Дата
Дизайнер	Кырлан А.С.			04.11.26

Проект: Квартира с кабинетом — М 1:20

Развёртки стен А1, Г. Коридор (пом. 5)

Стадия	Лист	Листов
П	93	127

Развёртка стены А2


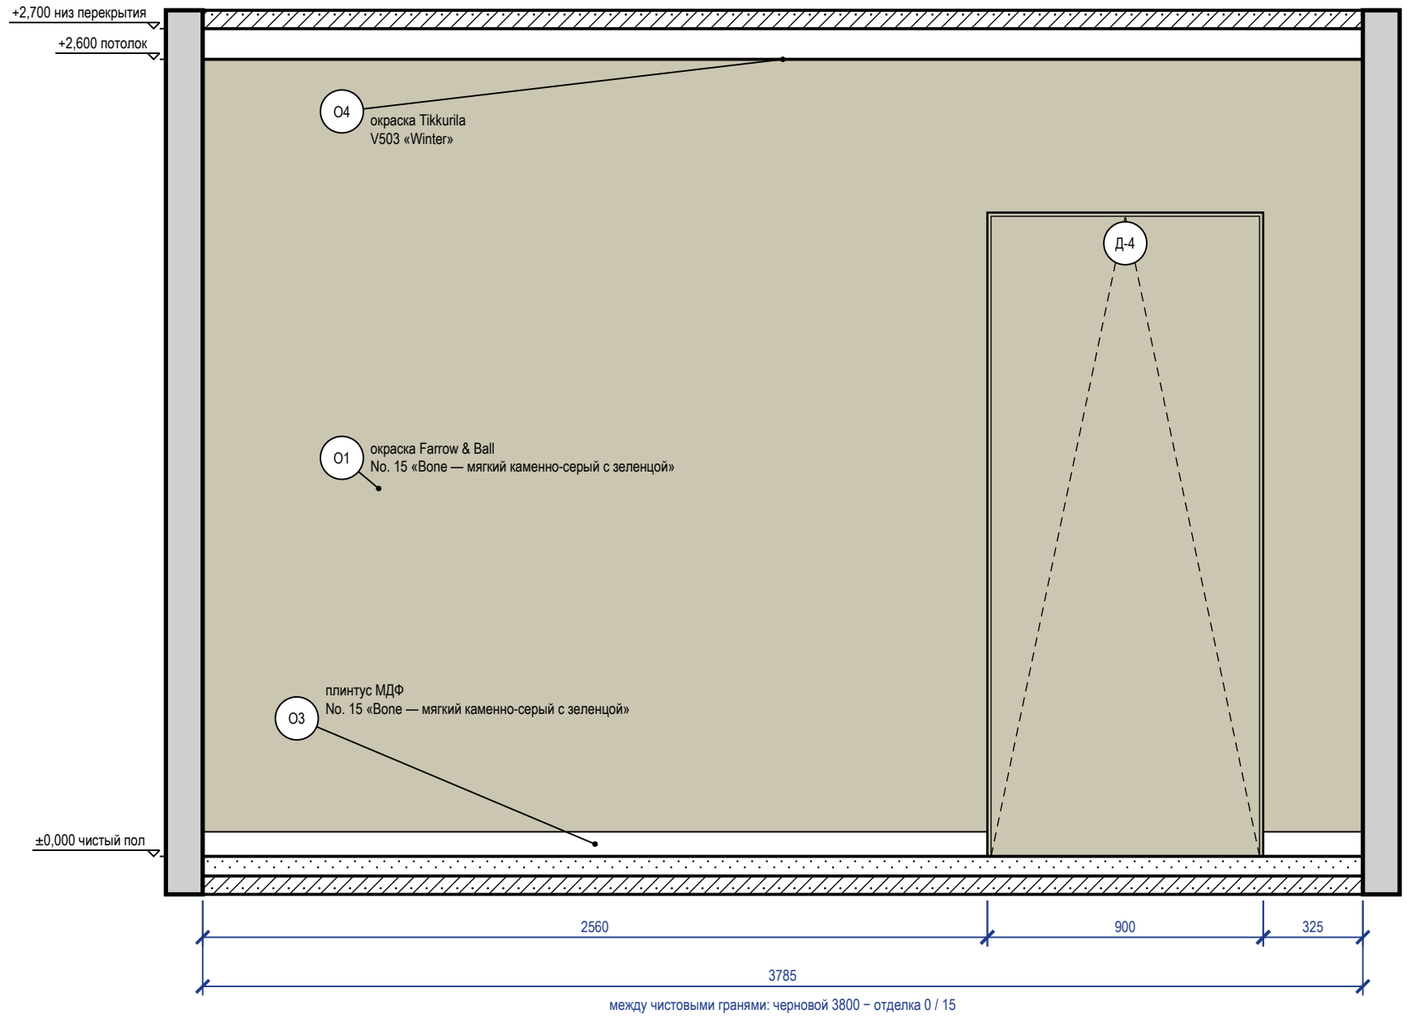


Схема развёрток (М 1:100)

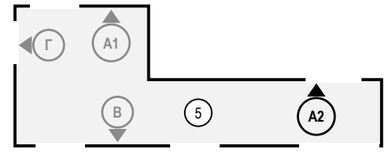

Ведомость отделки (на листе)

Марка	Поверхность	Материал, изделие	Цвет, код	Кол.
О1	стены	окраска, Farrow & Ball Modern Emulsion, матовая, подготовка Q3	Farrow & Ball No. 15 «Bone — мягкий каменно-серый с зеленцой»	8 м²
О3	плинтус	плинтус МДФ, h 80 мм, аналог: плинтус МДФ под покраску 80×16	Farrow & Ball No. 15 «Bone — мягкий каменно-серый с зеленцой»	2,9 м
О4	потолок	окраска, Tikkurila Anti-Reflex 2, глубокоматовая, подготовка Q3	Tikkurila V503 «Winter»	9,1 м²

Примечания

1. Размеры — в мм от чистовых поверхностей стен; условные обозначения и общие указания — лист 27.
2. Двери скрытого монтажа — полотно в плоскости стены, отделка стены по полотну, плинтус прерывается у короба (узел — на листе узлов).

					Проект: Квартира с кабинетом — М 1:20
	Лист	№ док.	Подпись	Дата	Развёртка стены А2. Коридор (пом. 5)
Дизайнер	Кырлан А.С.			04.11.26	Стадия: П · Лист: 94 · Листов: 127

выпуск 04.11.2026 № 627e1ac6ce · стр. 94 из 127

Развёртка стены В


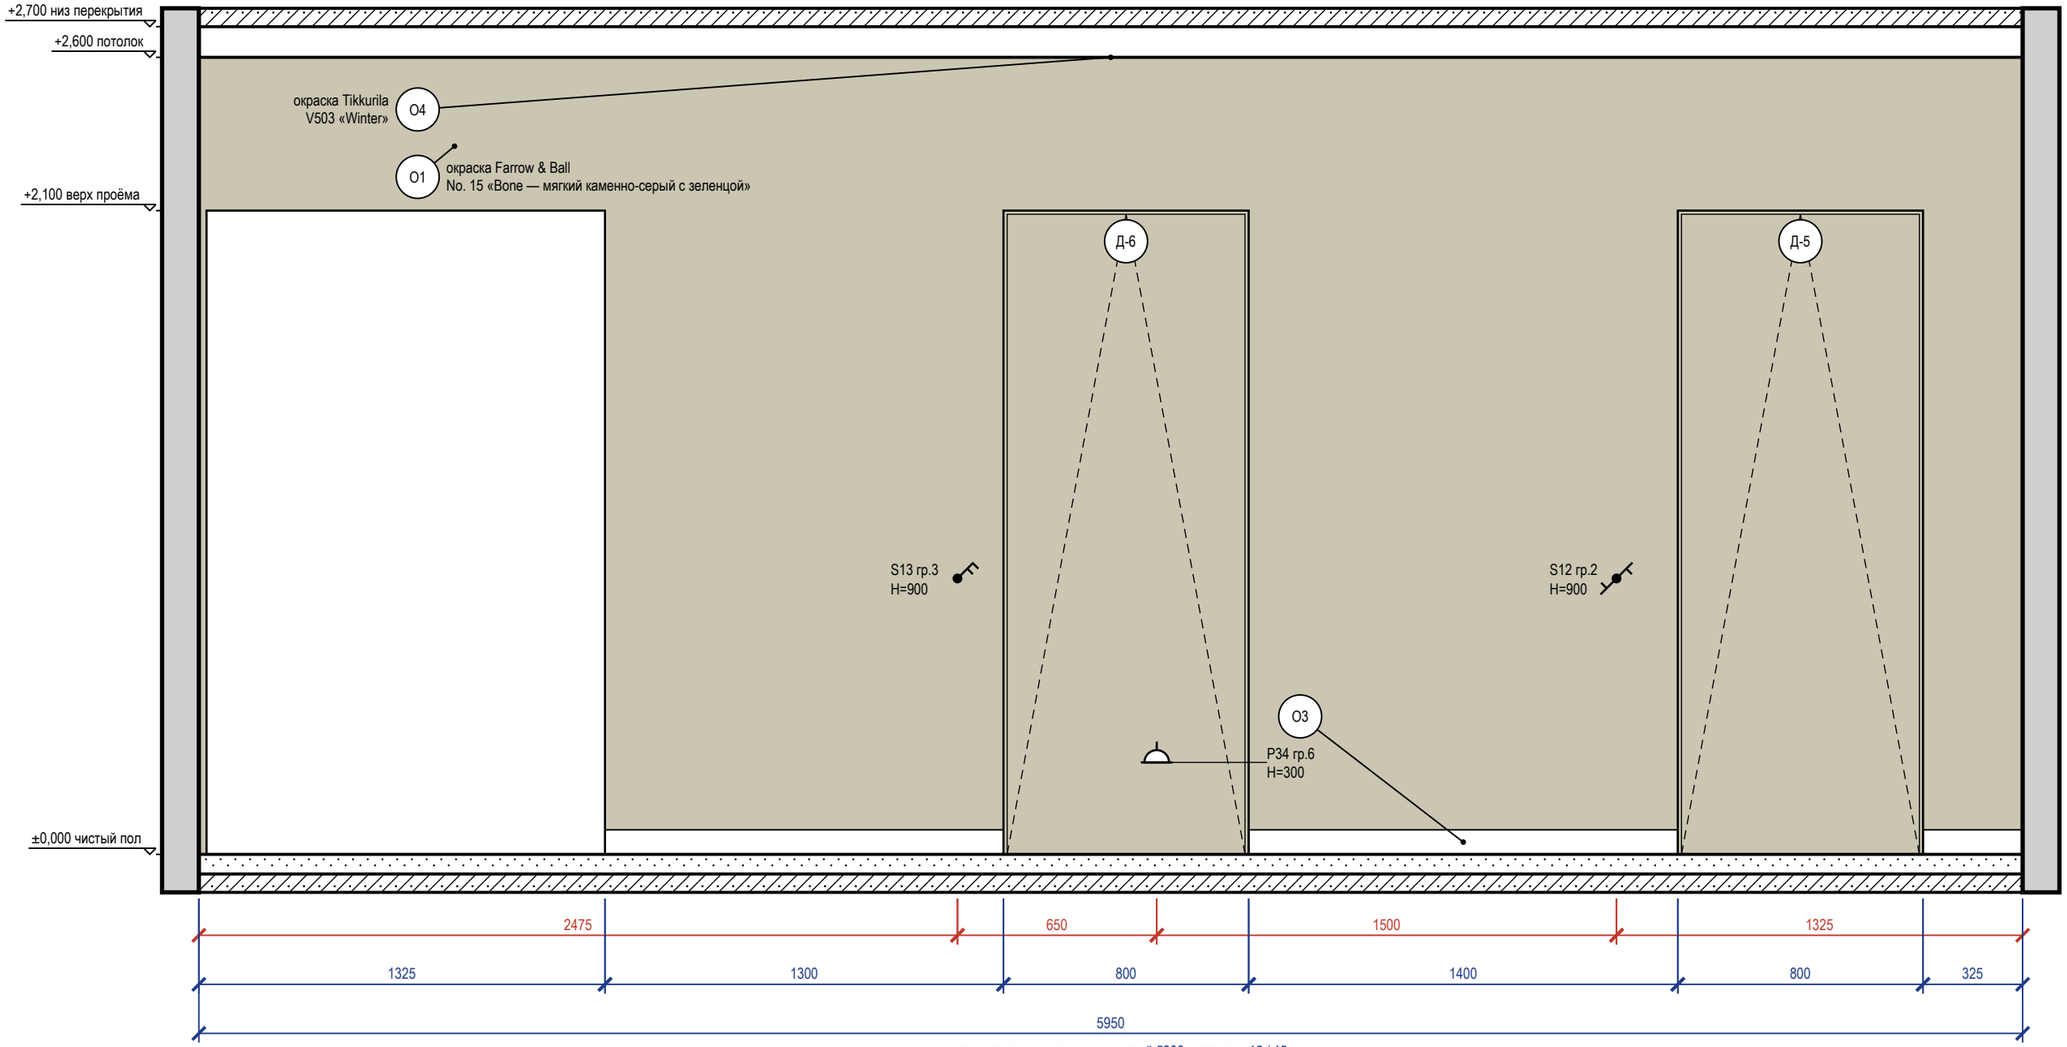



Схема развёрток (М 1:100)

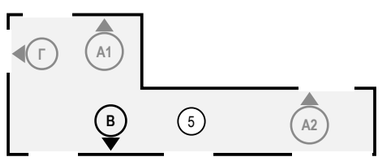

Ведомость отделки (на листе)

Марка	Поверхность	Материал, изделие	Цвет, код	Кол.
О1	стены	окраска, Farrow & Ball Modern Emulsion, матовая, подготовка Q3	Farrow & Ball No. 15 «Bone — мягкий каменно-серый с зеленцой»	9,4 м²
О3	плинтус	плинтус МДФ, h 80 мм, аналог: плинтус МДФ под покраску 80×16	Farrow & Ball No. 15 «Bone — мягкий каменно-серый с зеленцой»	3 м
О4	потолок	окраска, Tikkurila Anti-Reflex 2, глубокоматовая, подготовка Q3	Tikkurila V503 «Winter»	9,1 м²

Визуализация этой стены — лист 15

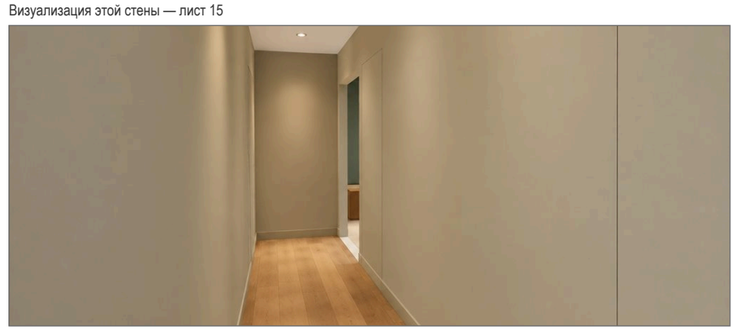

Примечания

1. Размеры — в мм от чистовых поверхностей стен; условные обозначения и общие указания — лист 27.
2. Двери скрытого монтажа — полотно в плоскости стены, отделка стены по полотну, плинтус прерывается у короба (узел — на листе узлов).


	Лист	№ док.	Подпись	Дата
Дизайнер	Кырлан А.С.			04.11.26

Проект: Квартира с кабинетом — М 1:20

Развёртка стены В. Коридор (пом. 5)


Стадия	Лист	Листов
П	95	127

Развёртка стены А

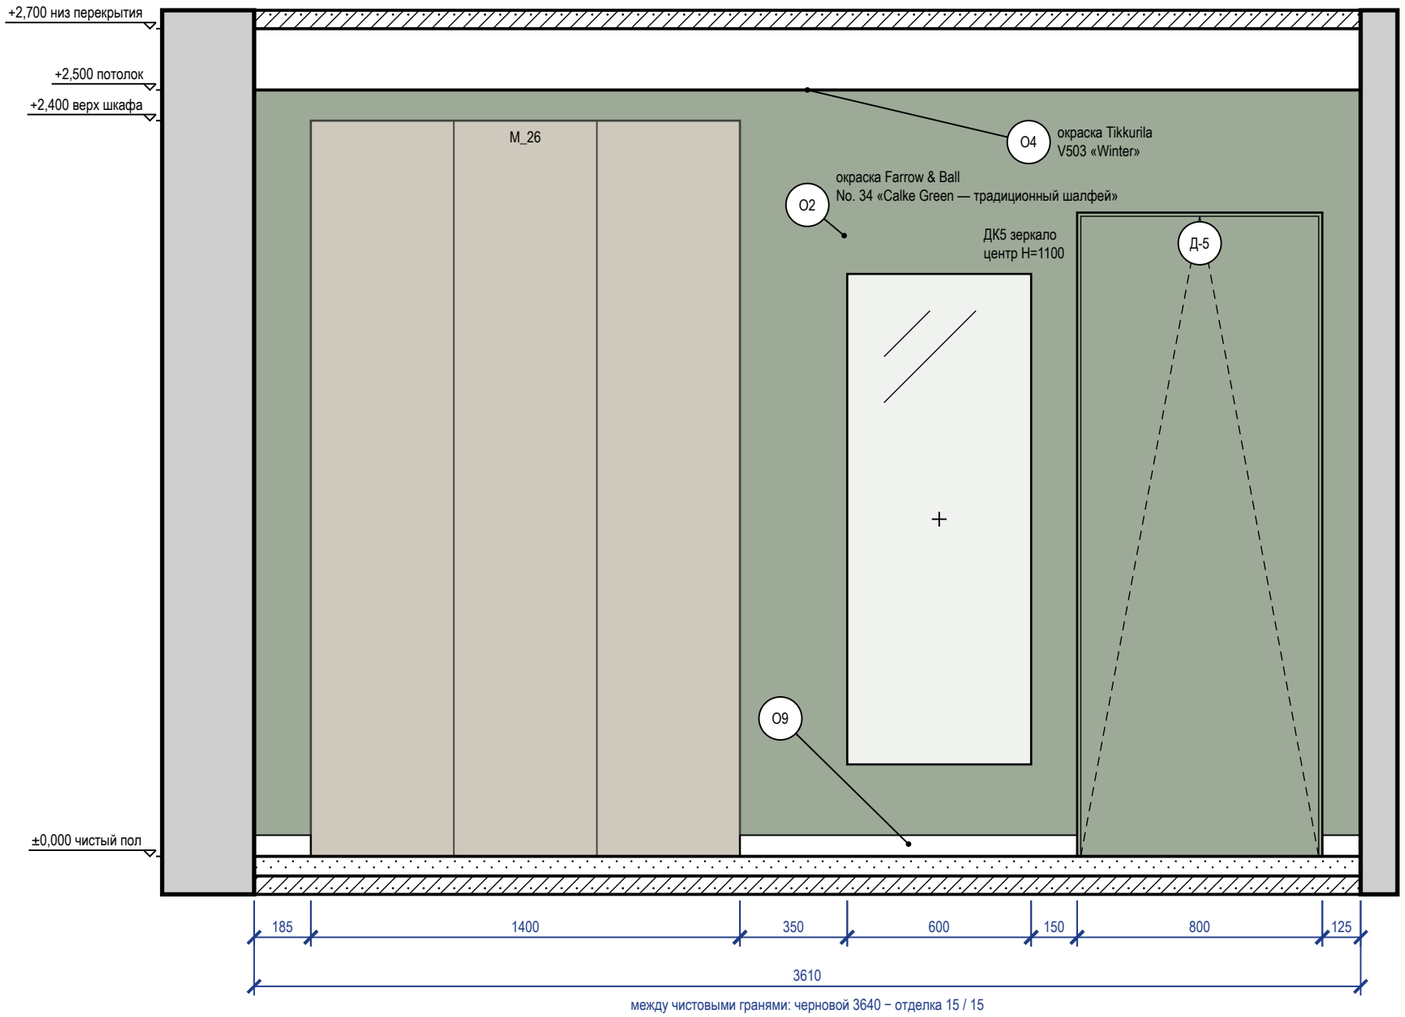

между чистовыми гранями: черновой 3640 − отделка 15 / 15

Схема развёрток (М 1:100)

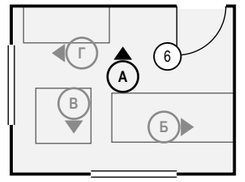

Ведомость отделки (на листе)

Марка	Поверхность	Материал, изделие	Цвет, код	Кол.
О2	акцентная стена	окраска, Farrow & Ball Modern Emulsion, матовая, подготовка Q3	Farrow & Ball No. 34 «Calke Green традиционный шалфей»	7,3 м²
О4	потолок	окраска, Tikkurila Anti-Reflex 2, глубокоматовая, подготовка Q3	Tikkurila V503 «Winter»	10 м²
О9	плинтус	плинтус МДФ, Orac Decor Contour (Luxxus), h 69 мм, SX165	Farrow & Ball No. 15 «Bone — мягкий каменно-серый с зеленцой»	1,4 м

Визуализация этой стены — лист 16



Примечания

1. Размеры — в мм от чистовых поверхностей стен; условные обозначения и общие указания — лист 27.
2. Картины и зеркала крепить к основанию по паспорту изделия (закладные и анкеры — в перечне скрытых работ); крест — ось центра предмета.
3. Двери скрытого монтажа — полотно в плоскости стены, отделка стены по полотну, плинтус прерывается у короба (узел — на листе узлов).
4. Потолок — у каждой стены свой, по плану потолков (ПТ1); ступени — зоной, кромка короба перед нишей — тонкой линией; в поле потолка: ПТ2 +2,600.

					Проект: Квартира с кабинетом	М 1:20
	Лист	№ док.	Подпись	Дата	Развёртка стены А. Детская (пом. 6)	Стадия / Лист / Листов
Дизайнер	Кырлан А.С.			04.11.26		П / 96 / 127

Развёртка стены Б


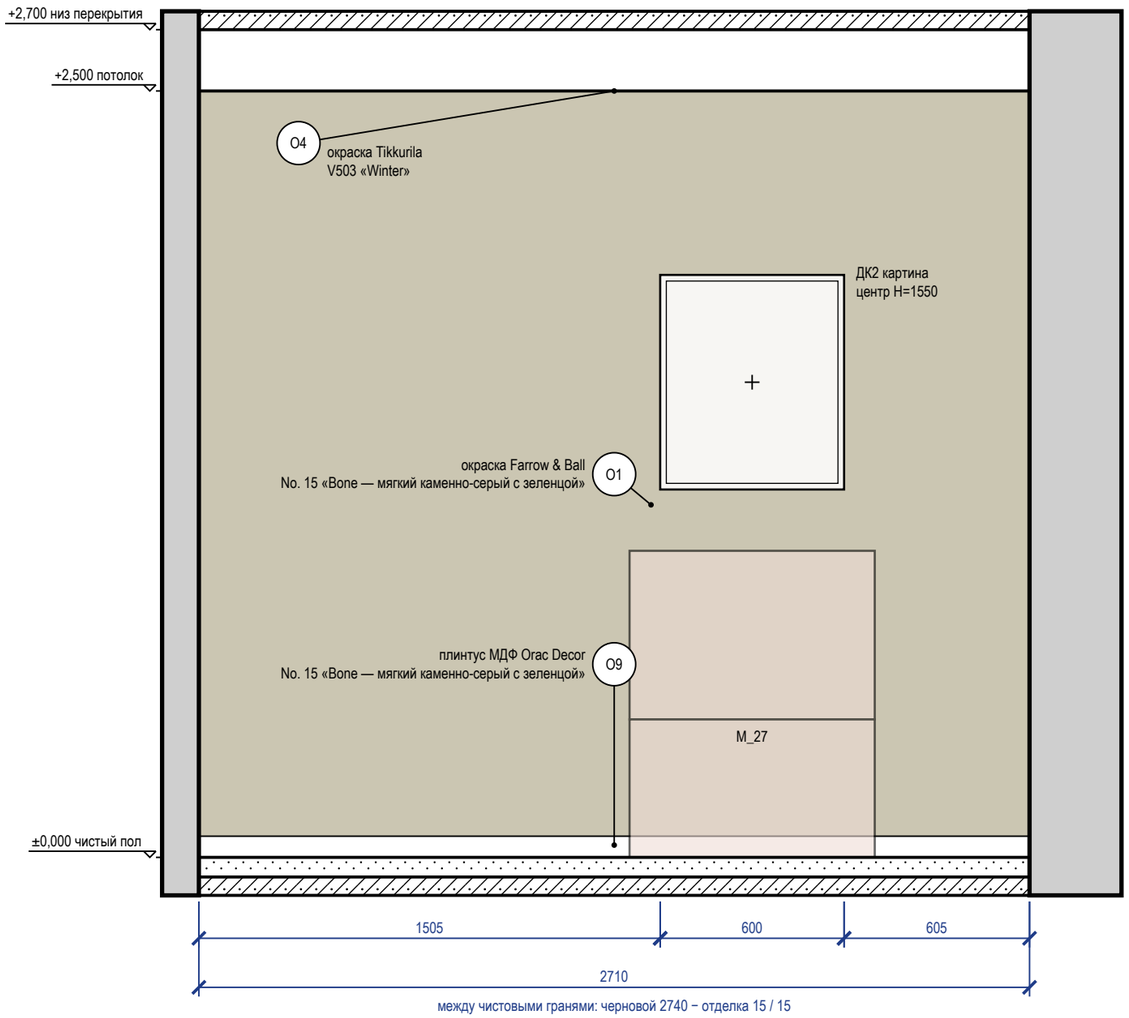



Схема развёрток (М 1:100)

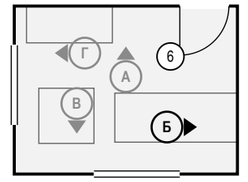

Ведомость отделки (на листе)

Марка	Поверхность	Материал, изделие	Цвет, код	Кол.
О1	стены	окраска, Farrow & Ball Modern Emulsion, матовая, подготовка Q3	Farrow & Ball No. 15 «Bone — мягкий каменно-серый с зеленцой»	6,8 м²
О4	потолок	окраска, Tikkurila Anti-Reflex 2, глубокоматовая, подготовка Q3	Tikkurila V503 «Winter»	10 м²
О9	плинтус	плинтус МДФ, Orac Decor Contour (Luxxus), h 69 мм, SX165	Farrow & Ball No. 15 «Bone — мягкий каменно-серый с зеленцой»	2,7 м

Визуализация этой стены — лист 17

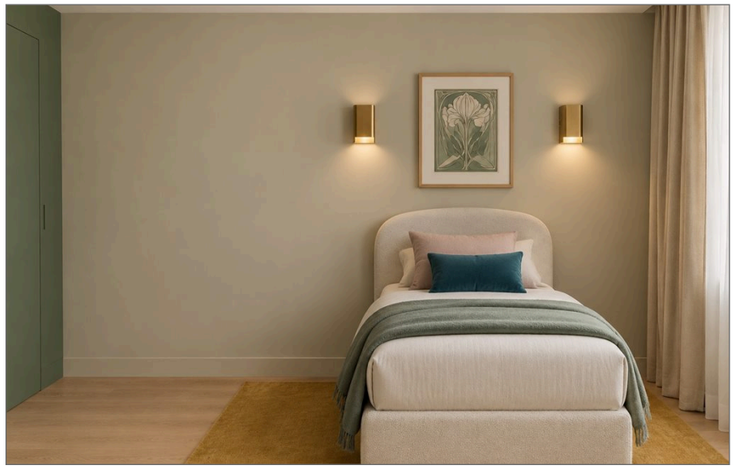

Примечания

1. Размеры — в мм от чистовых поверхностей стен; условные обозначения и общие указания — лист 27.
2. Стена Б показана двумя видами: здесь — архитектурная развёртка (мебель, отделка, проёмы, высоты), электроточки и выводы ВК с привязками и таблицей — на листе 98 («Привязки»).
3. Картины и зеркала крепить к основанию по паспорту изделия (закладные и анкеры — в перечне скрытых работ); крест — ось центра предмета.
4. Потолок — у каждой стены свой, по плану потолков (ПТ1); ступени — зоной, кромка короба перед нишей — тонкой линией; в поле потолка: ПТ2 +2,600.

					Проект: Квартира с кабинетом	М 1:20
	Лист	№ док.	Подпись	Дата		
Дизайнер	Кырлан А.С.			04.11.26	Развёртка стены Б. Детская (пом. 6)	Стадия: П; Лист: 97; Листов: 127

Развёртка стены Б: электроточки и выводы

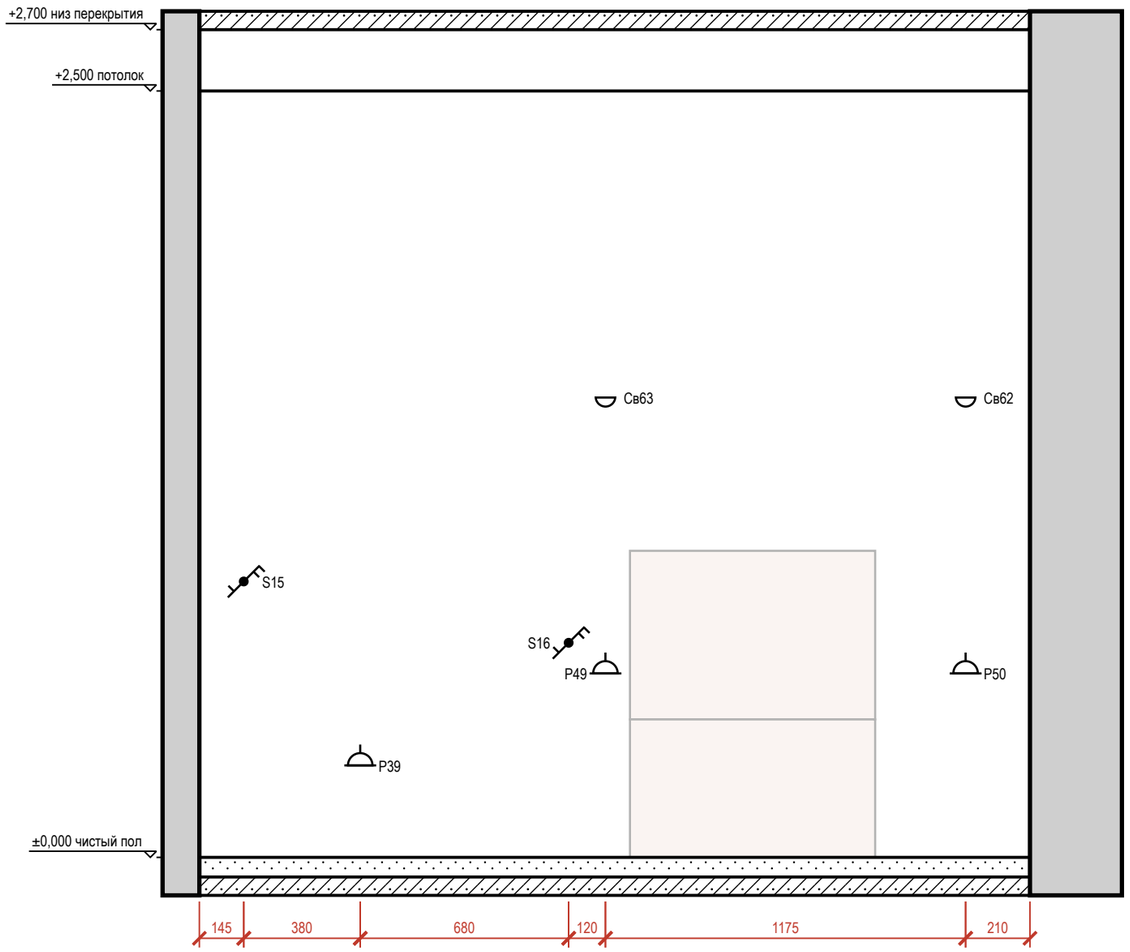



Таблица привязок электроточек и выводов

Марка	Назначение	От угла, мм	Н от пола, мм	Примечание
S15	выключатель	145	900	гр. 1
P39	розетка: уборка	525	300	гр. 5
S16	выключатель	1205	700	гр. 1
P49	розетка: у кровати	1325	600	гр. 5
Св63	светильник настенный	1325	1500	гр. 1
P50	розетка: у кровати	2500	600	гр. 5
Св62	светильник настенный	2500	1500	гр. 1

Условные обозначения

- розетка с заземляющим контактом; у знака — марка, ×N постов в рамке, гр. — группа щита, Н — высота оси, мм
- выключатель одноклавишный
- выключатель двухклавишный (флажков — по числу клавиш)
- выключатель с проходной или перекрёстной клавишей (обратный флажок); тип клавиши — в подписи
- светильник настенный (бра), Н — высота оси
- привязки точек и выводов от угла и от пола, мм
- марка развёртки: буква стены, стрелка — взгляд

Схема развёрток (М 1:50)

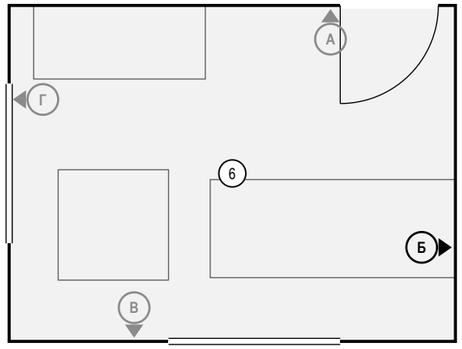

Примечания

1. Вид «Привязки» стены Б — электроточки и выводы ВК; архитектурная развёртка (мебель, отделка, проёмы, высоты) — на листе 97. Мебель и приборы — подложкой для ориентира; их марки и обозначения мебели, проёмов и стен — там же.
2. Привязки — в мм: по горизонтали от левого чистового угла стены до оси изделия, Н — от чистого пола до оси; все точки — в таблице привязок. Красная цепочка — привязки по осям; точки ближе 120 мм одна к другой в цепочку не дробятся — их привязки только в таблице.
3. У знака — марка электроточки (Р — розетка, S — выключатель, Св — светильник, ЭВ — вывод кабеля); условные обозначения и общие указания — лист 27.

					Проект: Квартира с кабинетом — **М 1:20**
	Лист	№ док.	Подпись	Дата	Привязки электроточек, стена Б. Детская (пом. 6)
Дизайнер	Кырлан А.С.			04.11.26	Стадия: П · Лист: 98 · Листов: 127

Развёртка стены В


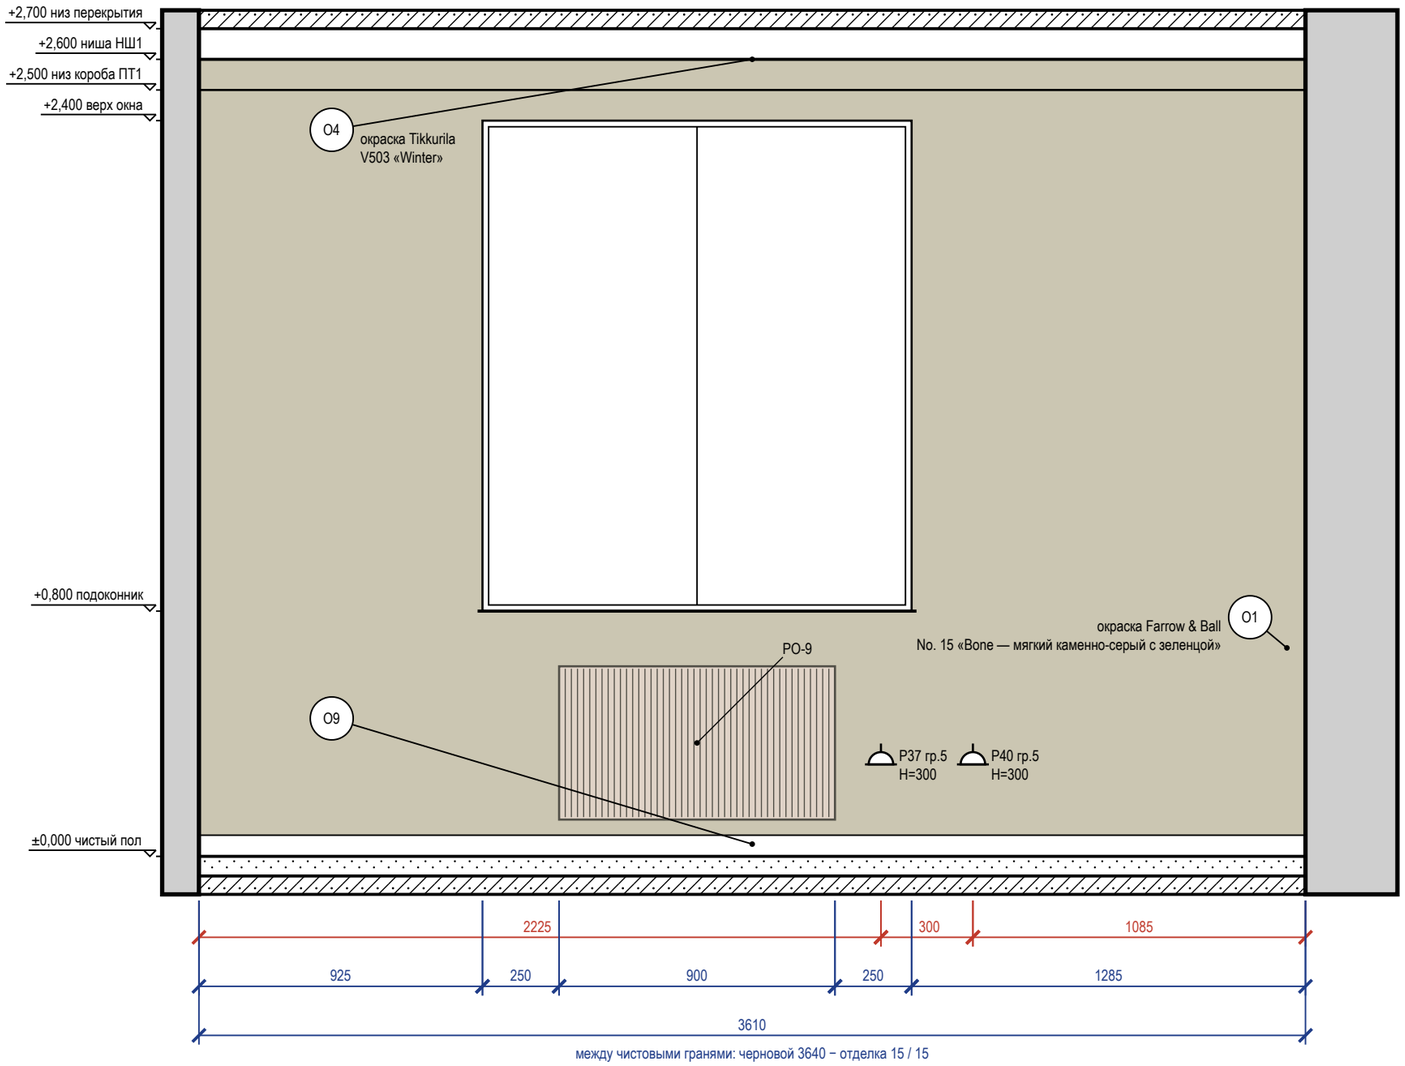


Схема развёрток (М 1:100)

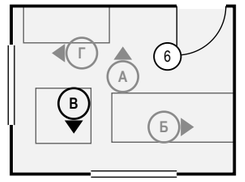

Ведомость отделки (на листе)

Марка	Поверхность	Материал, изделие	Цвет, код	Кол.
О1	стены	окраска, Farrow & Ball Modern Emulsion, матовая, подготовка Q3	Farrow & Ball No. 15 «Bone — мягкий каменно-серый с зеленцой»	7,1 м²
О4	потолок	окраска, Tikkurila Anti-Reflex 2, глубокоматовая, подготовка Q3	Tikkurila V503 «Winter»	10 м²
О9	плинтус	плинтус МДФ, Orac Decor Contour (Luxxus), h 69 мм, SX165	Farrow & Ball No. 15 «Bone — мягкий каменно-серый с зеленцой»	3,6 м

Примечания

1. Размеры — в мм от чистовых поверхностей стен; условные обозначения и общие указания — лист 27.
2. Потолок — у каждой стены свой, по плану потолков (НШ1, ПТ1); ступени — зоной, кромка короба перед нишей — тонкой линией; в поле потолка: ПТ2 +2,600.

					Проект: Квартира с кабинетом — М 1:20
	Лист	№ док.	Подпись	Дата	Развёртка стены В. Детская (пом. 6)
Дизайнер	Кырлан А.С.			04.11.26	Стадия: П; Лист: 99; Листов: 127

Развёртка стены Г


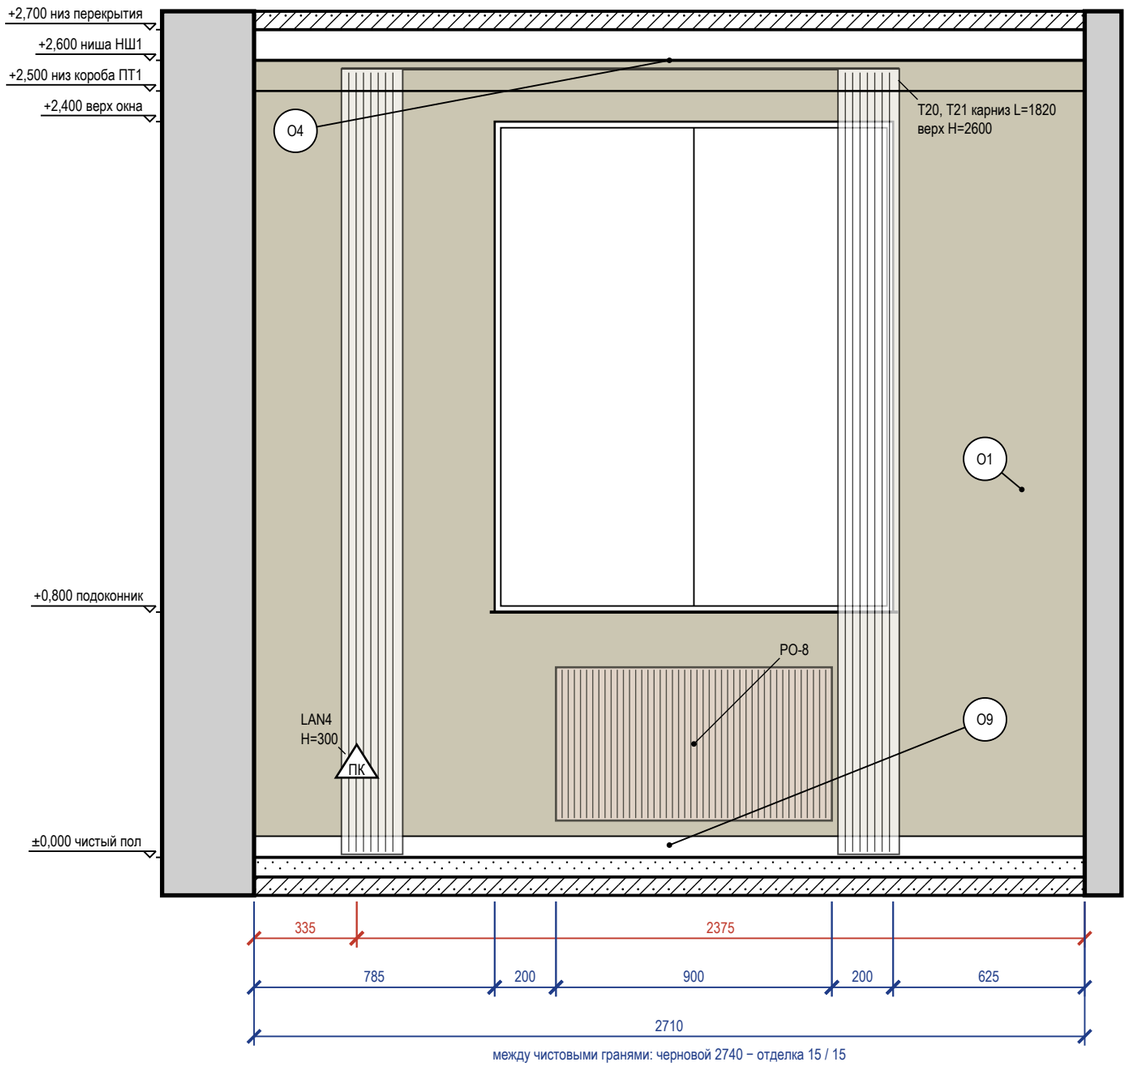


Схема развёрток (М 1:100)

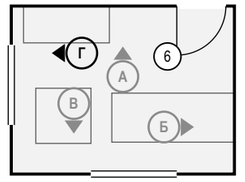

Ведомость отделки (на листе)

Марка	Поверхность	Материал, изделие	Цвет, код	Кол.
О1	стены	окраска, Farrow & Ball Modern Emulsion, матовая, подготовка Q3	Farrow & Ball No. 15 «Bone — мягкий каменно-серый с зеленцой»	5 м²
О4	потолок	окраска, Tikkurila Anti-Reflex 2, глубокоматовая, подготовка Q3	Tikkurila V503 «Winter»	10 м²
О9	плинтус	плинтус МДФ, Orac Decor Contour (Luxxus), h 69 мм, SX165	Farrow & Ball No. 15 «Bone — мягкий каменно-серый с зеленцой»	2,7 м

Визуализация этой стены — лист 18




Примечания

1. Размеры — в мм от чистовых поверхностей стен; условные обозначения и общие указания — лист 27.
2. Карнизы (шины) — по ведомости текстиля декоратора: длина L и верх H на развёртке — те же числа, что в ведомости; крепление — до окраски потолка.
3. Потолок — у каждой стены свой, по плану потолков (НШ1, ПТ1); ступени — зоной, кромка короба перед нишей — тонкой линией; в поле потолка: ПТ2 +2,600.


					Проект: Квартира с кабинетом	М 1:20
	Лист	№ док.	Подпись	Дата		
Дизайнер	Кырлан А.С.			04.11.26	Развёртка стены Г. Детская (пом. 6)	Стадия: П; Лист: 100; Листов: 127

Развёртка стены А

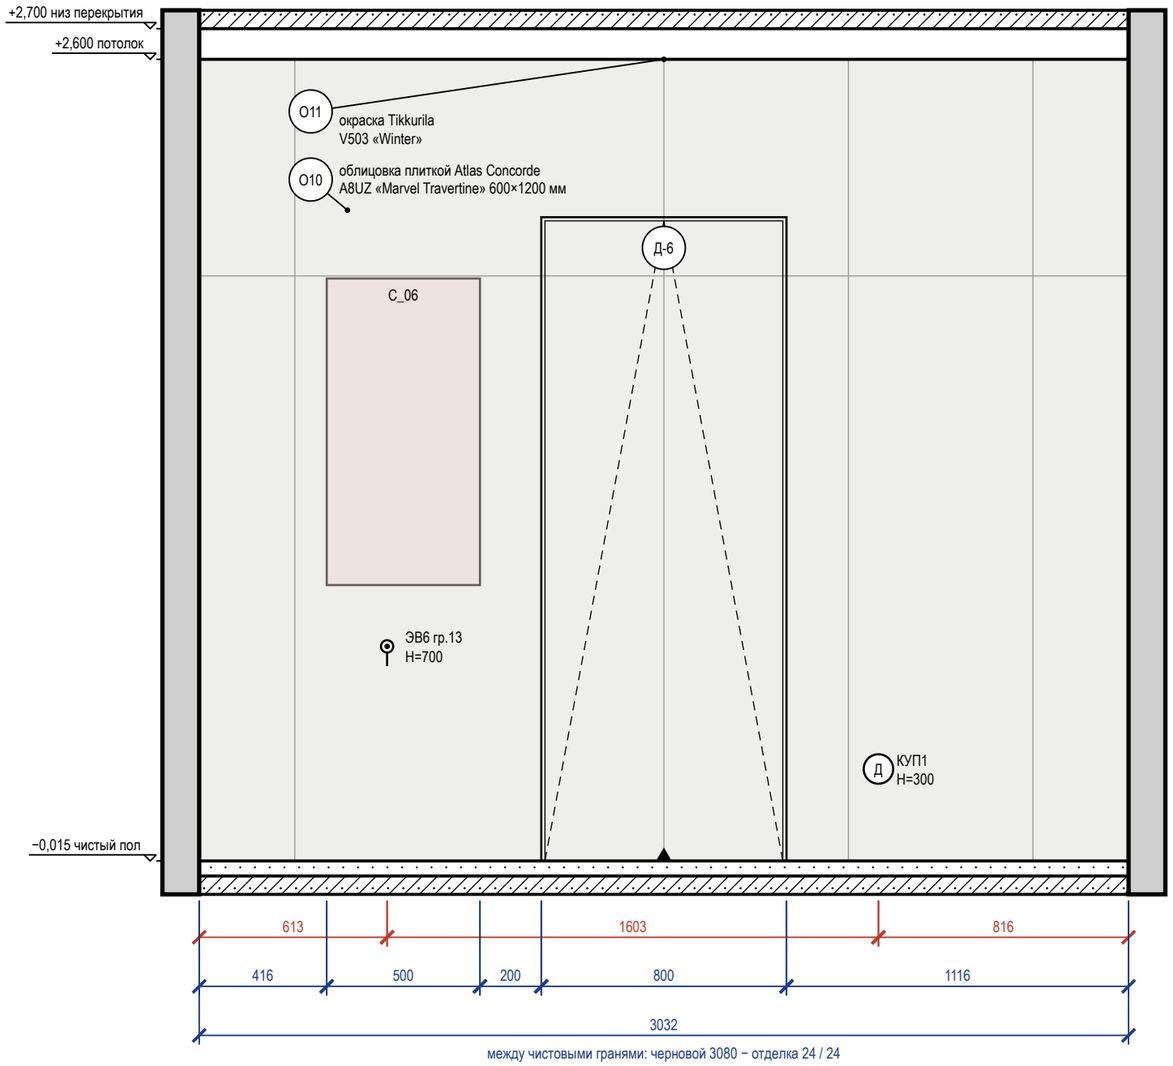


между чистовыми гранями: черновой 3080 − отделка 24 / 24

Развёртка стены Б

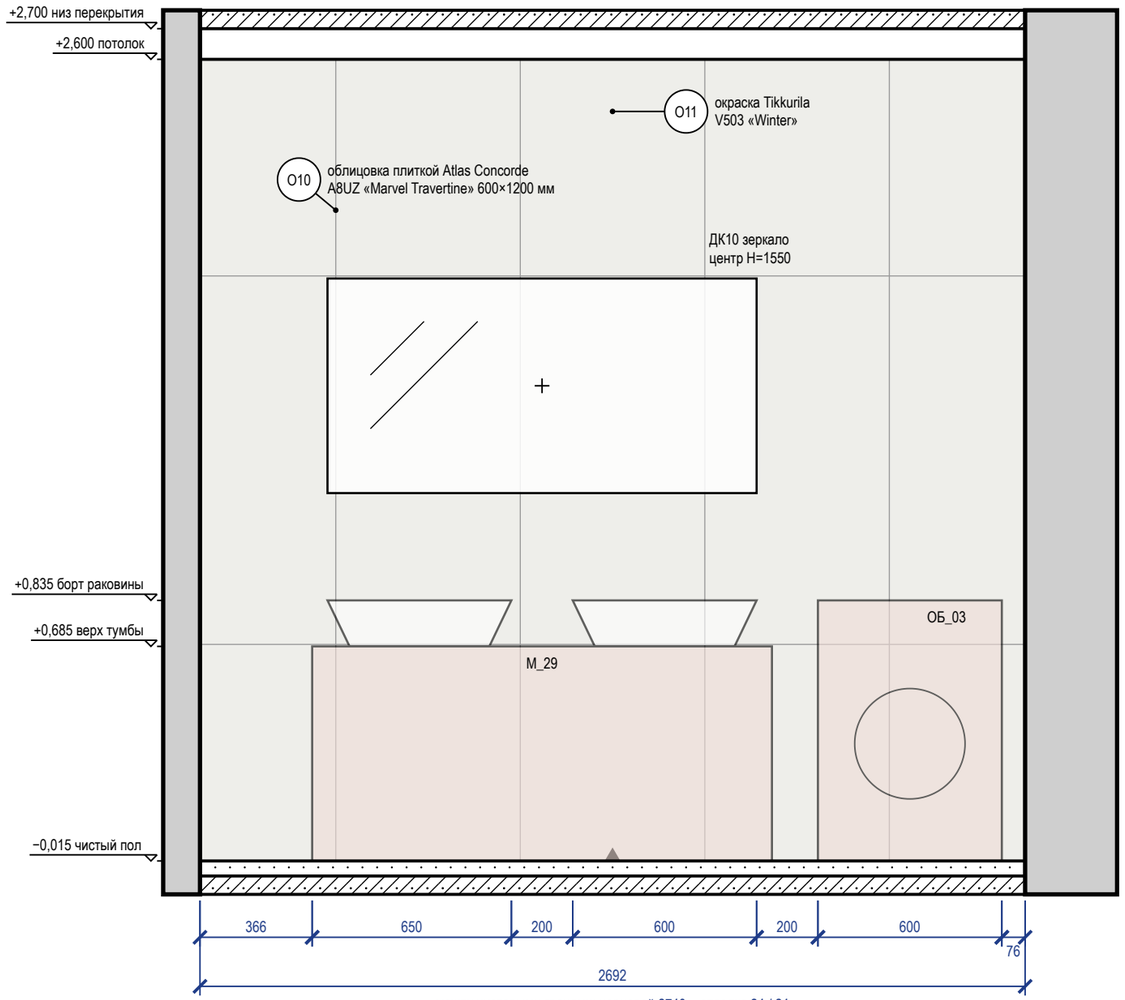

между чистовыми гранями: черновой 2740 − отделка 24 / 24

Схема развёрток (М 1:100)

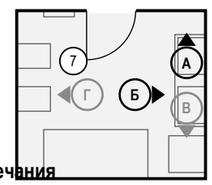

Ведомость отделки (на листе)

Марка	Поверхность	Материал, изделие	Цвет, код	Кол.
О10	стены	облицовка плиткой, Atlas Concorde Marvel Travertine, 600×1200×9 мм, A8UZ, затирка CG2WA	Atlas Concorde A8UZ «Marvel Travertine»	13,3 м²
О11	потолок	окраска, Tikkurila Luja 7, матовая, подготовка Q3	Tikkurila V503 «Winter»	8,4 м²

Визуализация этой стены — лист 19




Примечания

1. Размеры — в мм от чистовых поверхностей стен; условные обозначения и общие указания — лист 27.
2. Стена Б показана двумя видами: здесь — архитектурная развёртка (мебель, отделка, проёмы, высоты), электроточки и выводы ВК с привязками и таблицей — на листе 103 («Привязки»).
3. Схема мебели, приборов и декора не является технической документацией для производства мебели; габариты — по паспортам изделий.
4. Облицовка — по сетке швов 2 мм, раскладка от оси стены (треугольник у пола), по высоте — от середины облицовки, подрезки у пола и у потолка поровну; подрезки — по листу раскладки плитки.
5. Гидроизоляция в 2 слоя, заход на стены 200 мм; над ванной — до 2000 и 300 мм за борт — до облицовки, с актом скрытых работ и тестом проливом (узел — на листе узлов).
6. Картины и зеркала крепить к основанию по паспорту изделия (закладные и анкеры — в перечне скрытых работ); крест — ось центра предмета.
7. Двери скрытого монтажа — полотно в плоскости стены, отделка стены по полотну, плинтус прерывается у короба (узел — на листе узлов).


					Проект: Квартира с кабинетом	М 1:20
	Лист	№ док.	Подпись	Дата	Развёртки стен А, Б. Ванная (пом. 7)	Стадия: П; Лист: 101; Листов: 127
Дизайнер	Кырлан А.С.			04.11.26		

Развёртка стены В

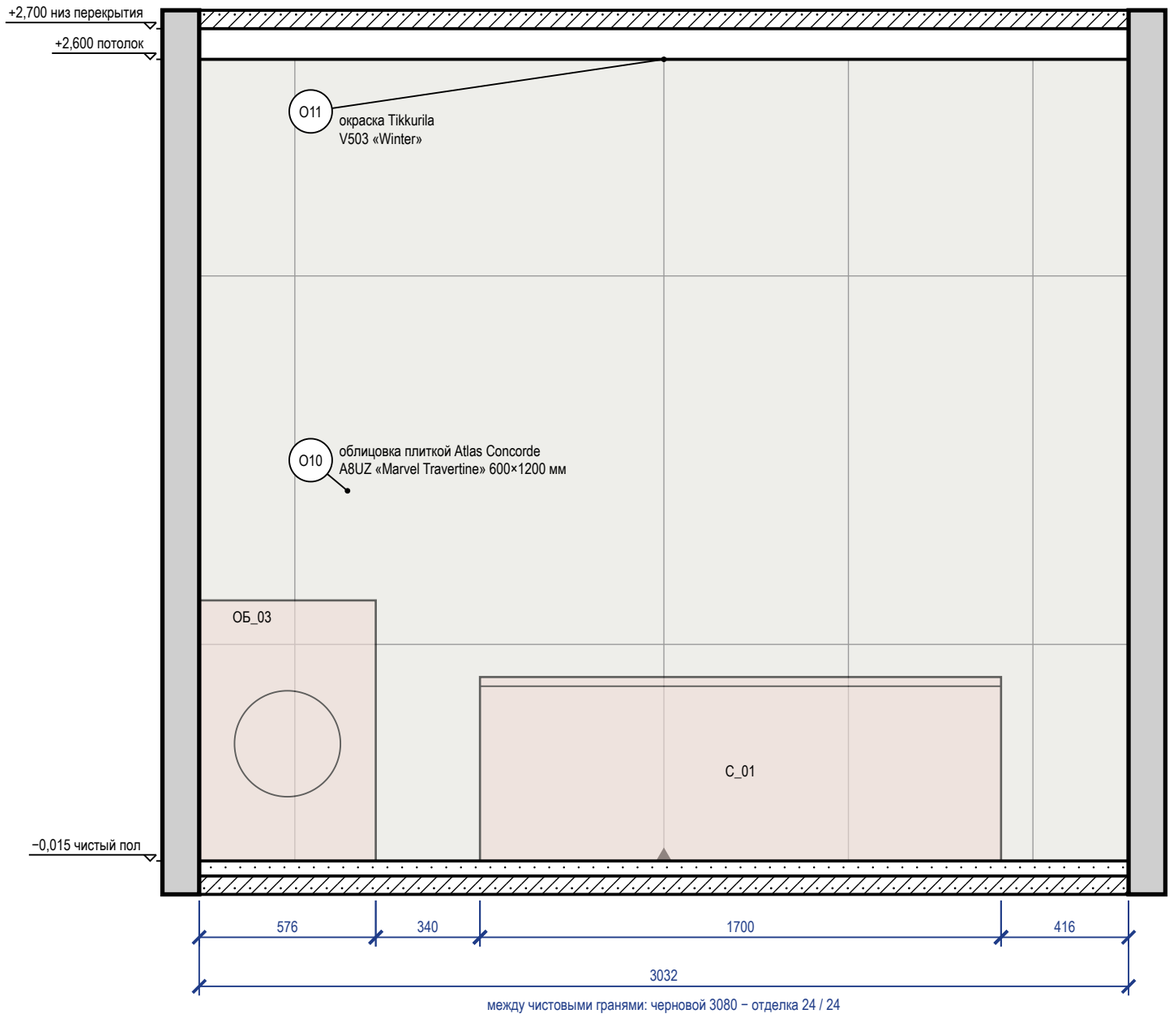


между чистовыми гранями: черновой 3080 − отделка 24 / 24

Развёртка стены Г

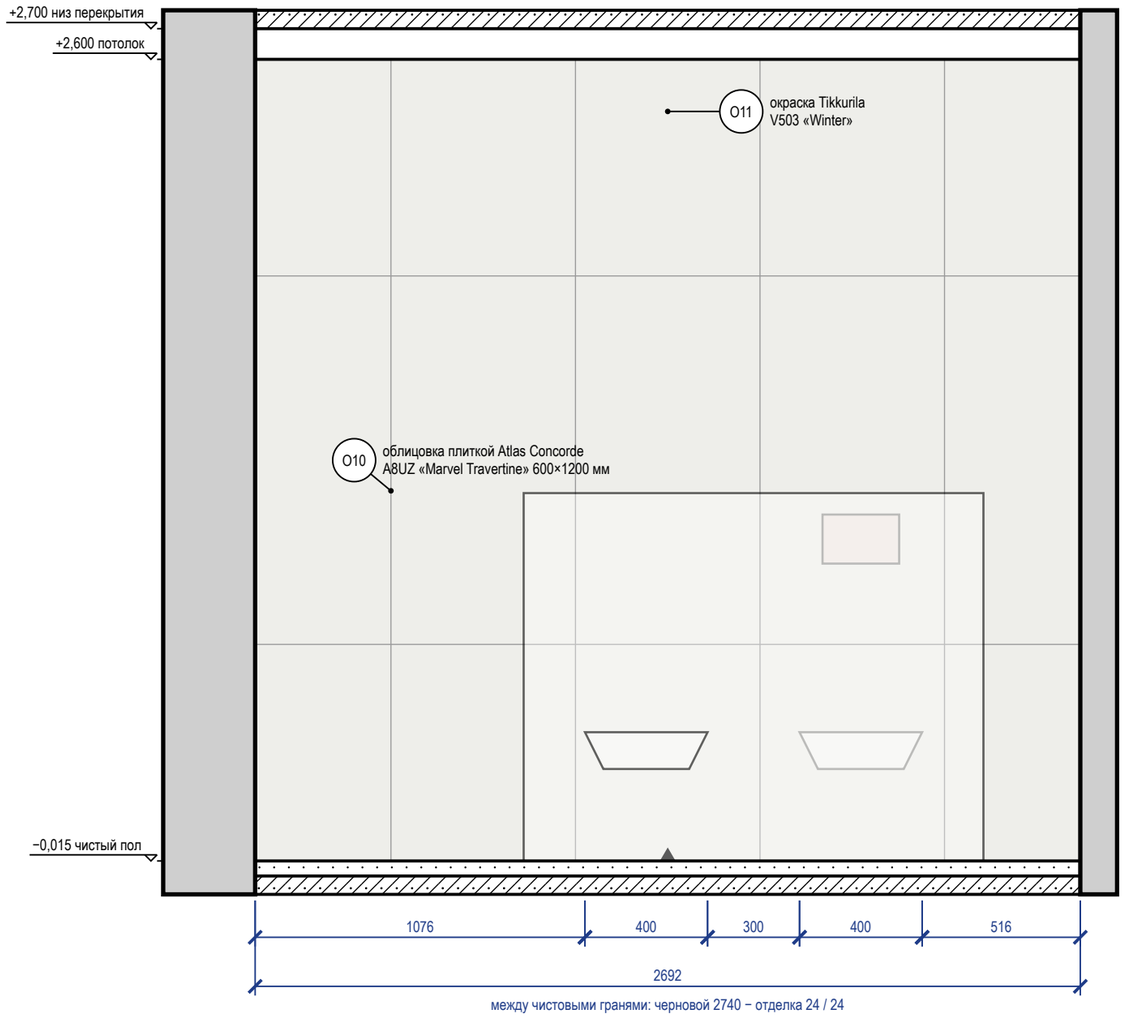

между чистовыми гранями: черновой 2740 − отделка 24 / 24

Схема развёрток (М 1:100)

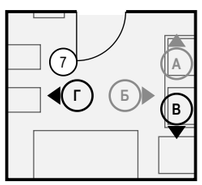

Ведомость отделки (на листе)

Марка	Поверхность	Материал, изделие	Цвет, код	Кол.
О10	стены	облицовка плиткой, Atlas Concorde Marvel Travertine, 600×1200×9 мм, A8UZ, затирка CG2WA	Atlas Concorde A8UZ «Marvel Travertine»	15 м²
О11	потолок	окраска, Tikkurila Luja 7, матовая, подготовка Q3	Tikkurila V503 «Winter»	8,4 м²

Визуализация этой стены — лист 20




Примечания

1. Размеры — в мм от чистовых поверхностей стен; условные обозначения и общие указания — лист 27.
2. Стена Г показана двумя видами: здесь — архитектурная развёртка (мебель, отделка, проёмы, высоты), электроточки и выводы ВК с привязками и таблицей — на листе 103 («Привязки»).
3. Схема мебели, приборов и декора не является технической документацией для производства мебели; габариты — по паспортам изделий.
4. Облицовка — по сетке швов 2 мм, раскладка от оси стены (треугольник у пола), по высоте — от середины облицовки, подрезки у пола и у потолка поровну; подрезки — по листу раскладки плитки.
5. Гидроизоляция в 2 слоя, заход на стены 200 мм; над ванной — до 2000 и 300 мм за борт — до облицовки, с актом скрытых работ и тестом проливом (узел — на листе узлов).

					Проект: Квартира с кабинетом	М 1:20
	Лист	№ док.	Подпись	Дата		
Дизайнер	Кырлан А.С.			04.11.26	Развёртки стен В, Г. Ванная (пом. 7)	Стадия: П; Лист: 102; Листов: 127

Развёртка стены Б: электроточки и выводы

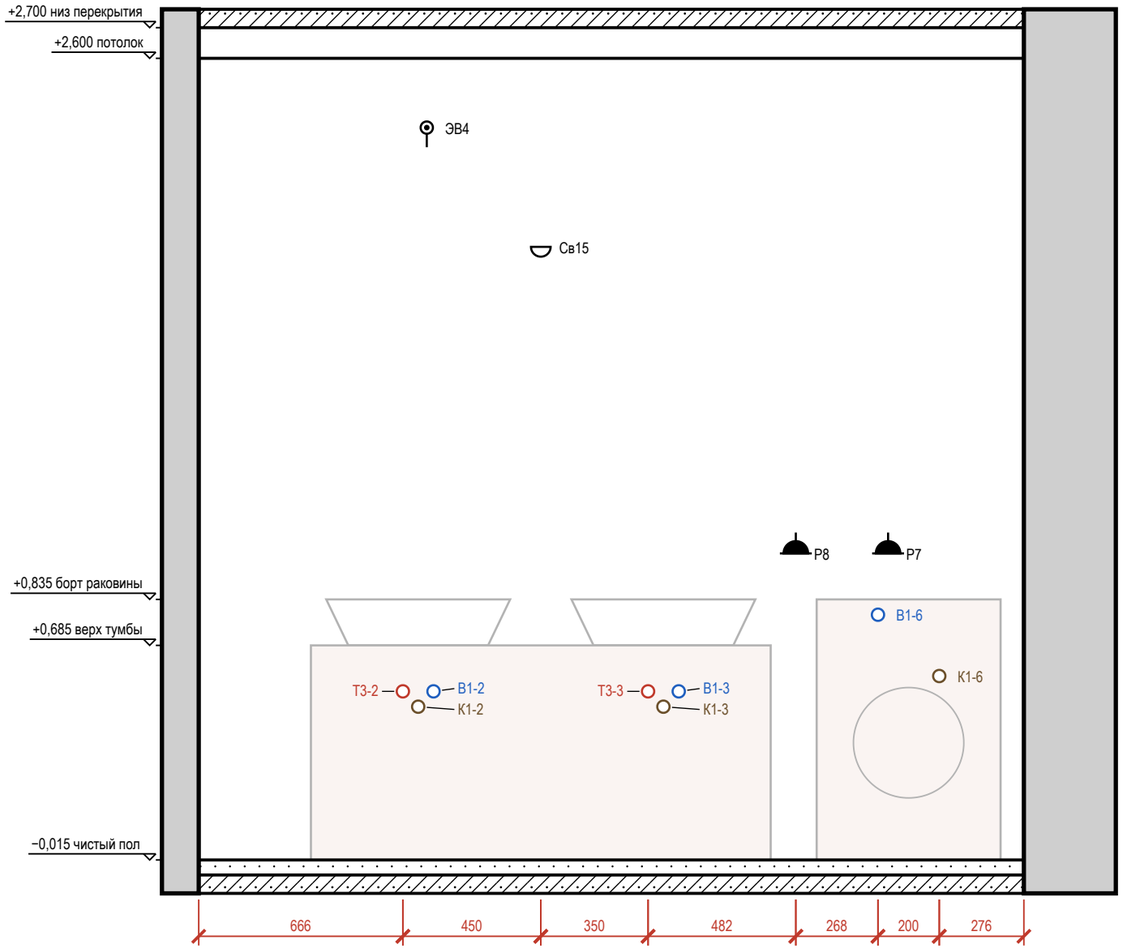

Развёртка стены Г: электроточки и выводы

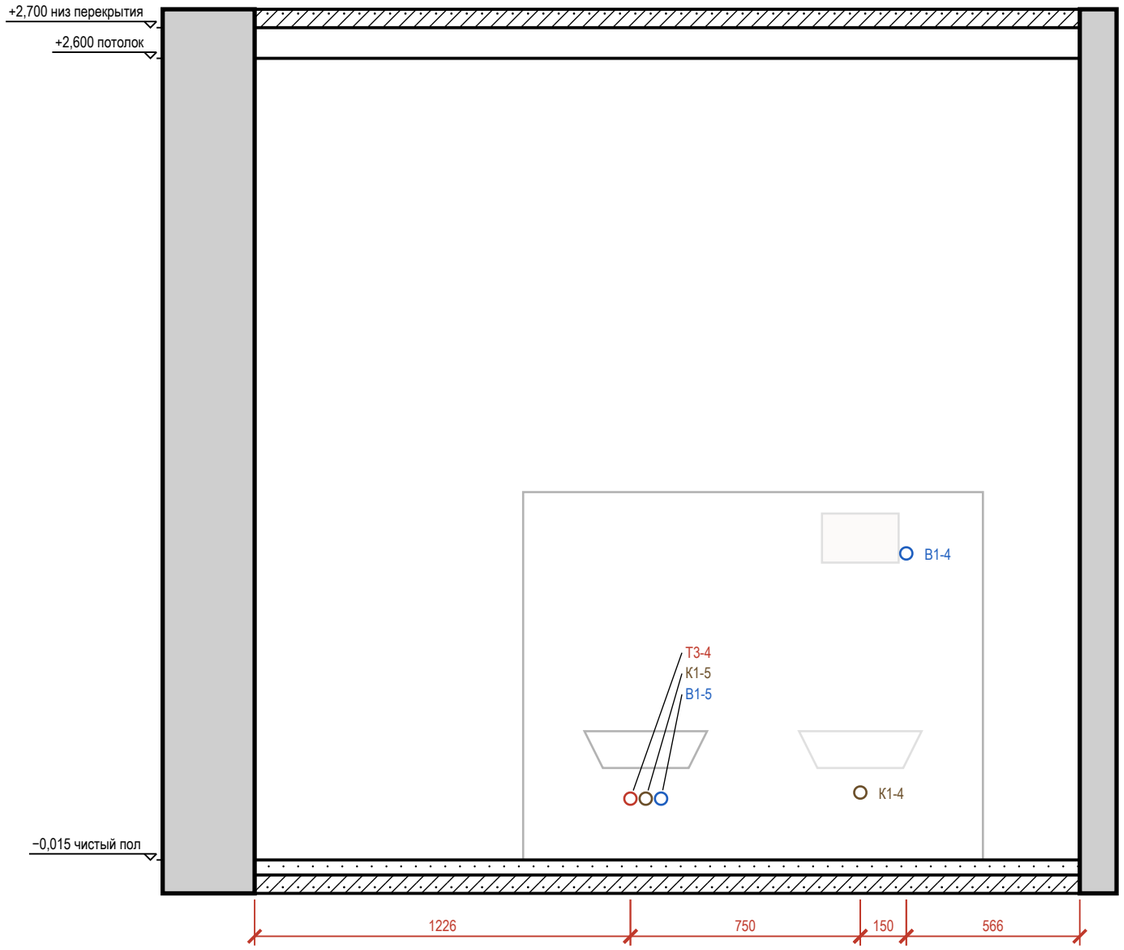


Таблица привязок электроточек и выводов

Стена	Марка	Назначение	От угла, мм	H от пола, мм	Примечание
Б	T3-2	горячая вода — умывальник	666	550	межос. 100
Б	K1-2	канализация — умывальник	716	500	Ø50
Б	ЭВ4	вывод кабеля: вентилятор ВР1 (таймер выбега)	744	2389	гр. 3
Б	B1-2	холодная вода — умывальник	766	550	межос. 100
Б	Св15	светильник настенный	1116	2000	гр. 3
Б	T3-3	горячая вода — умывальник	1466	550	межос. 100
Б	K1-3	канализация — умывальник	1516	500	Ø50
Б	B1-3	холодная вода — умывальник	1566	550	межос. 100
Б	P8	розетка: фен у умывальника	1948	1000	гр. 13, IP44

Стена	Марка	Назначение	От угла, мм	H от пола, мм	Примечание
Б	B1-6	холодная вода — стиральная машина	2216	800	кран машины
Б	P7	розетка: стиральная машина	2249	1000	гр. 12, IP44
Б	K1-6	канализация — стиральная машина	2416	600	Ø50
Г	T3-4	горячая вода — биде подвесное	1226	200	межос. 100, в раме
Г	K1-5	канализация — биде подвесное	1276	200	Ø50
Г	B1-5	холодная вода — биде подвесное	1326	200	межос. 100, в раме
Г	K1-4	канализация — унитаз подвесной	1976	220	Ø110
Г	B1-4	холодная вода — унитаз подвесной	2126	1000	в раме инсталляции

Условные обозначения

- розетка влагозащищённая IP44
- вывод кабеля для подключения прибора (без розетки), марка ЭВ
- светильник настенный (бра), H — высота оси
- вывод B1 (код — в ведомости привязок)
- вывод T3 (код — в ведомости привязок)
- вывод K1 (код — в ведомости привязок)
- привязки точек и выводов от угла и от пола, мм


Примечания

1. Вид «Привязки» стен Б, Г — электроточки и выводы ВК; архитектурная развёртка (мебель, отделка, проёмы, высоты) — на листах 101, 102. Мебель и приборы подложкой для ориентира; их марки и обозначения мебели, проёмов и стен — там же.
2. Привязки — в мм: по горизонтали от левого чистового угла стены до оси изделия, H — от чистого пола до оси; все точки — в таблице привязок. Красная цепочка — привязки по осям; точки ближе 120 мм одна к другой в цепочку не дробятся — их привязки только в таблице.
3. У знака — марка электроточки (P — розетка, S — выключатель, Св — светильник, ЭВ — вывод кабеля); условные обозначения и общие указания — лист 27.
4. Коды выводов ВК: B1 — холодная вода, T3 — горячая вода, K1 — канализация; номер после дефиса — номер вывода на листе выводов сантехники.

					Проект: Квартира с кабинетом — **М 1:20**
	Лист	№ док.	Подпись	Дата	Привязки электроточек и выводов ВК, стены Б, Г. Ванная (пом. 7)
Дизайнер	Кырлан А.С.			04.11.26	Стадия: П; Лист: 103; Листов: 127


выпуск 04.11.2026 № 627e1ac6ce · стр. 103 из 127

Развёртка стены Б

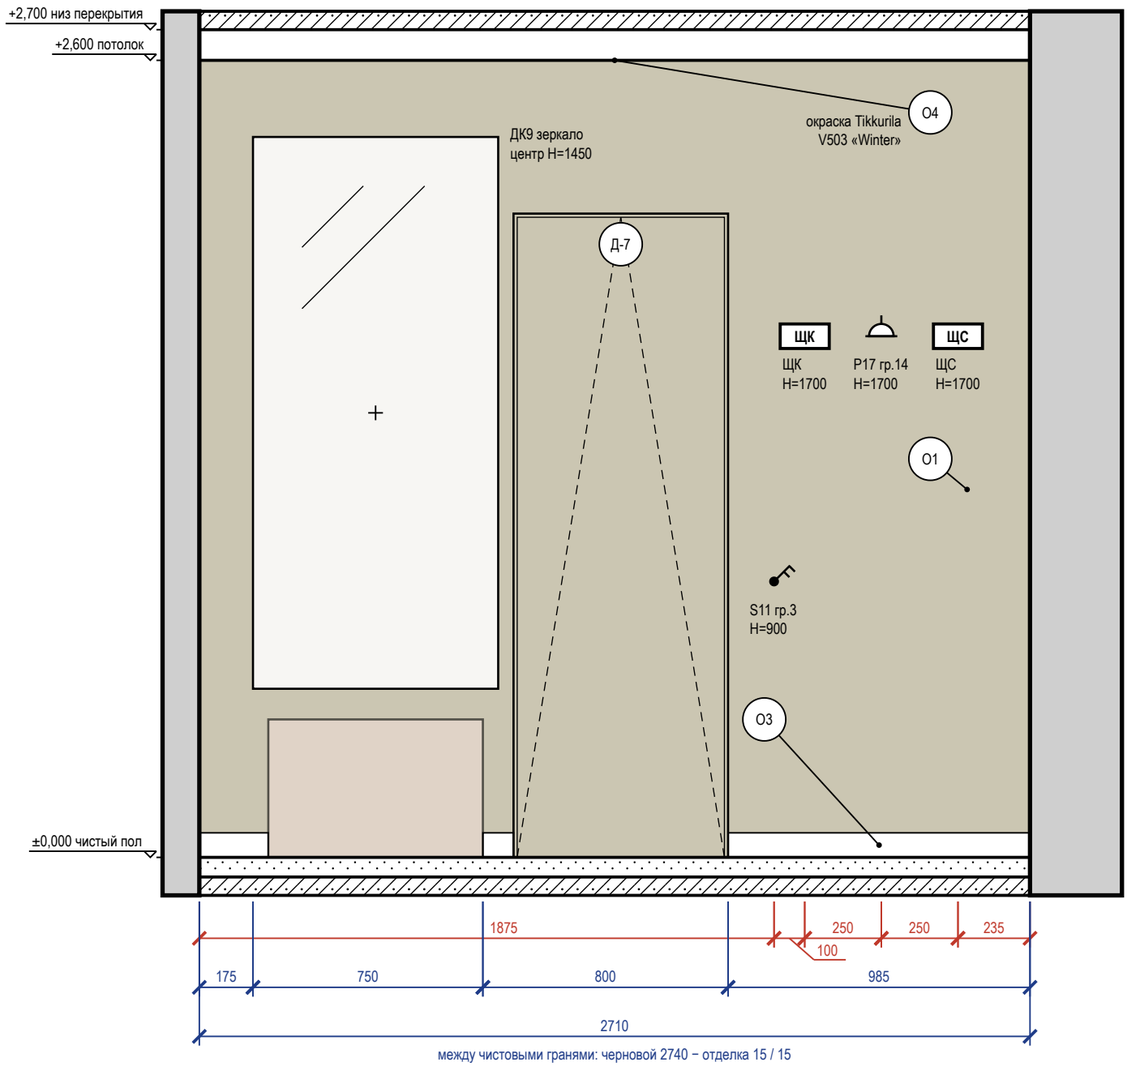


между чистовыми гранями: черновой 2740 − отделка 15 / 15

Развёртка стены В

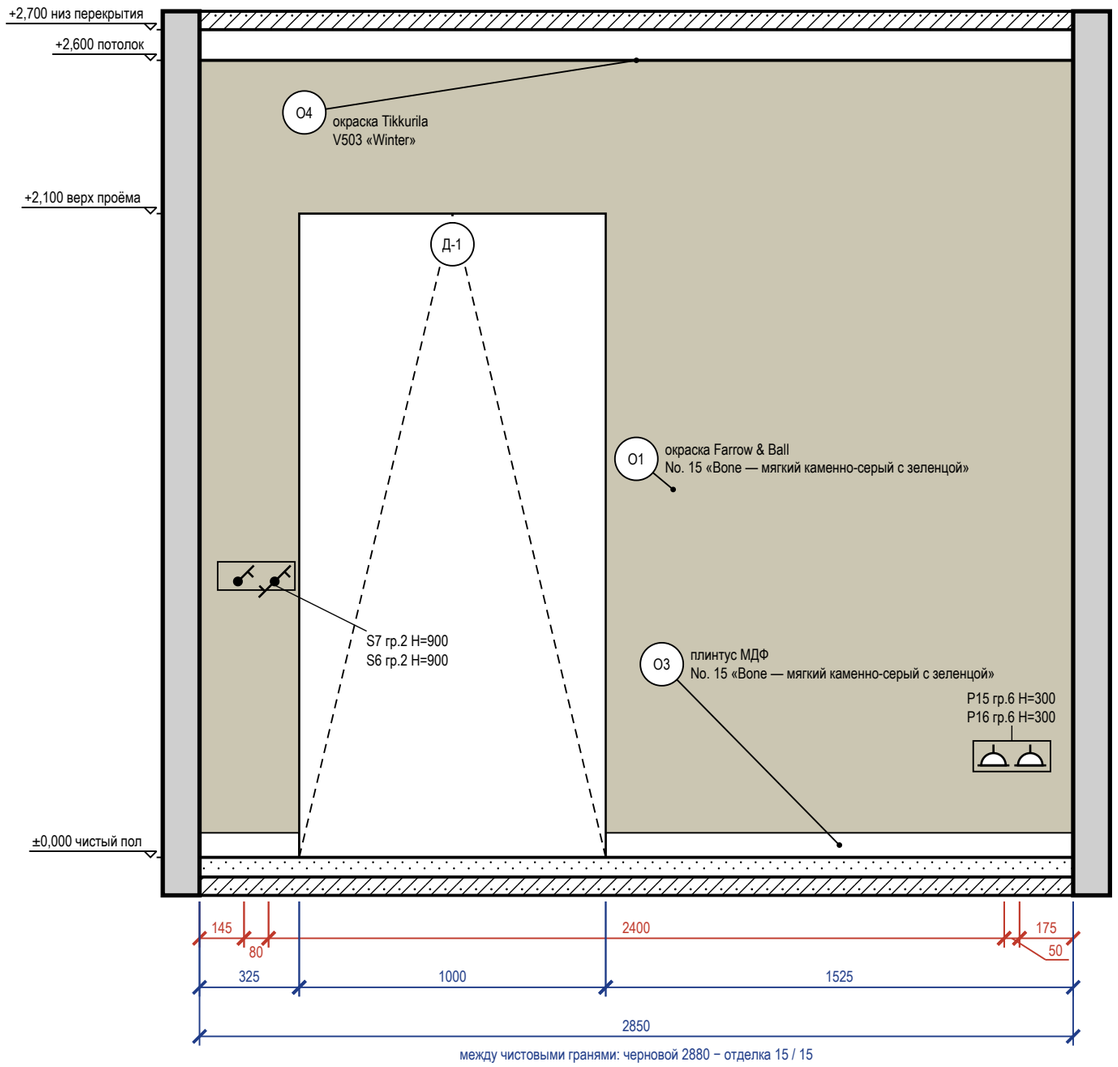

между чистовыми гранями: черновой 2880 − отделка 15 / 15


Схема развёрток (М 1:100)

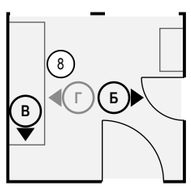

Ведомость отделки (на листе)

Марка	Поверхность	Материал, изделие	Цвет, код	Кол.
О1	стены	окраска, Farrow & Ball Modern Emulsion, матовая, подготовка Q3	Farrow & Ball No. 15 «Bone — мягкий каменно-серый с зеленцой»	10,9 м²
О3	плинтус	плинтус МДФ, h 80 мм, аналог: плинтус МДФ под покраску 80×16	Farrow & Ball No. 15 «Bone — мягкий каменно-серый с зеленцой»	3,2 м
О4	потолок	окраска, Tikkurila Anti-Reflex 2, глубокоматовая, подготовка Q3	Tikkurila V503 «Winter»	7,9 м²

Визуализация этой стены — лист 22

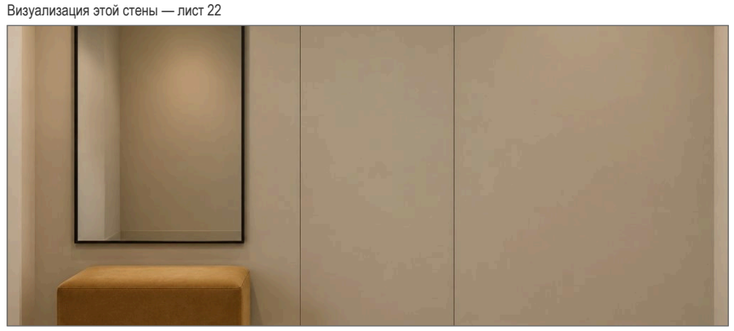

Примечания

1. Размеры — в мм от чистовых поверхностей стен; условные обозначения и общие указания — лист 27.
2. Картины и зеркала крепить к основанию по паспорту изделия (закладные и анкеры — в перечне скрытых работ); крест — ось центра предмета.
3. Двери скрытого монтажа — полотно в плоскости стены, отделка стены по полотну, плинтус прерывается у короба (узел — на листе узлов).

					Проект: Квартира с кабинетом	М 1:20
	Лист	№ док.	Подпись	Дата	Развёртки стен Б, В. Прихожая (пом. 8)	Стадия / Лист / Листов
Дизайнер	Кырлан А.С.			04.11.26		П / 104 / 127

выпуск 04.11.2026 № 627e1ac6ce · стр. 104 из 127

Развёртка стены Г


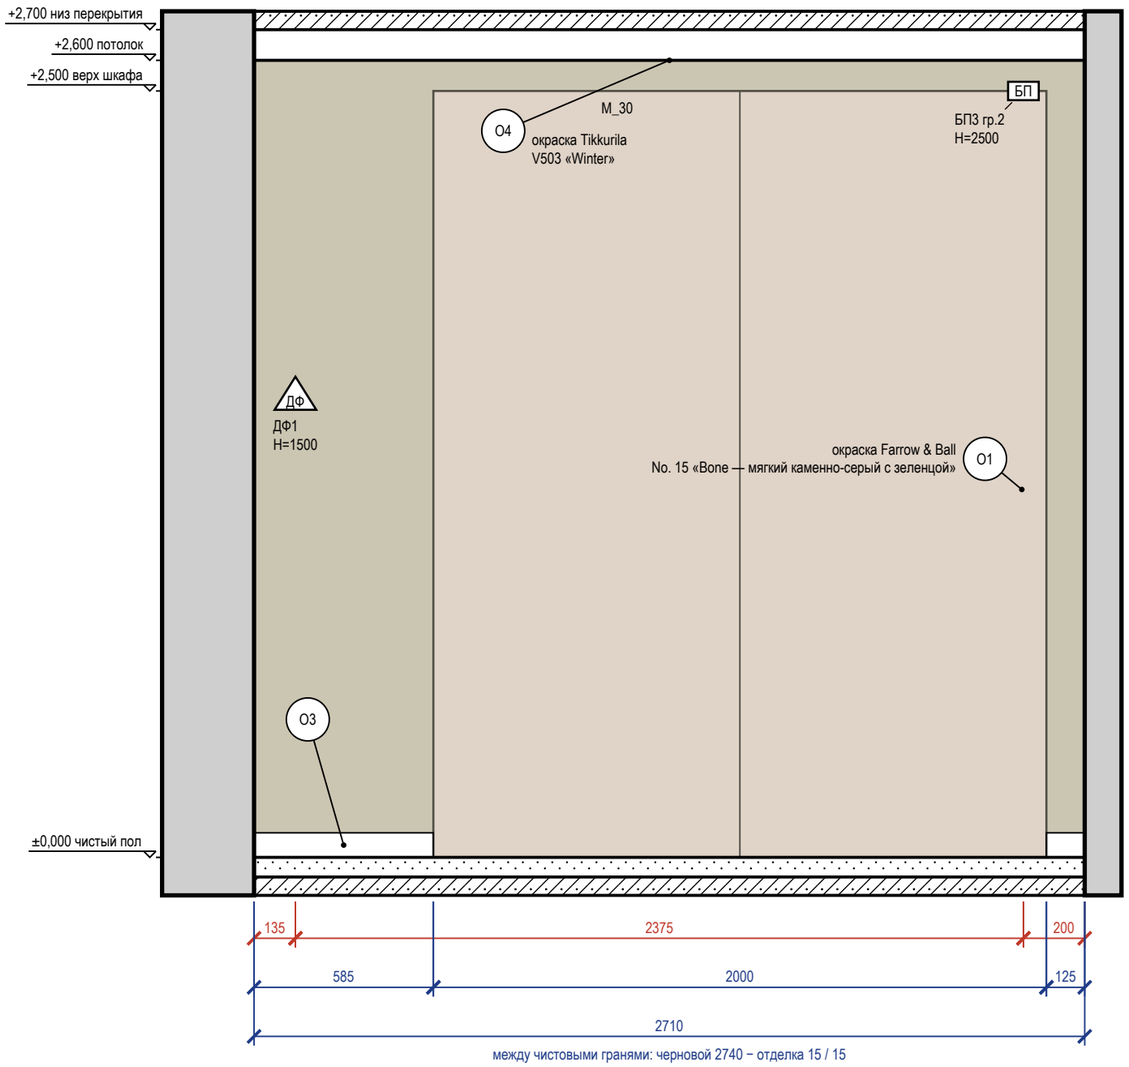


Схема развёрток (М 1:100)

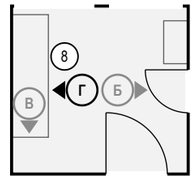

Ведомость отделки (на листе)

Марка	Поверхность	Материал, изделие	Цвет, код	Кол.
О1	стены	окраска, Farrow & Ball Modern Emulsion, матовая, подготовка Q3	Farrow & Ball No. 15 «Bone — мягкий каменно-серый с зеленцой»	7 м²
О3	плинтус	плинтус МДФ, h 80 мм, аналог: плинтус МДФ под покраску 80×16	Farrow & Ball No. 15 «Bone — мягкий каменно-серый с зеленцой»	0,7 м
О4	потолок	окраска, Tikkurila Anti-Reflex 2, глубокоматовая, подготовка Q3	Tikkurila V503 «Winter»	7,9 м²

Визуализация этой стены — лист 24




Примечания

1. Размеры — в мм от чистовых поверхностей стен; условные обозначения и общие указания — лист 27.

	Лист	№ док.	Подпись	Дата	Проект: Квартира с кабинетом — М 1:20
Дизайнер	Кырлан А.С.			04.11.26	Развёртка стены Г. Прихожая (пом. 8)

Стадия	Лист	Листов
П	105	127

Развёртка стены А

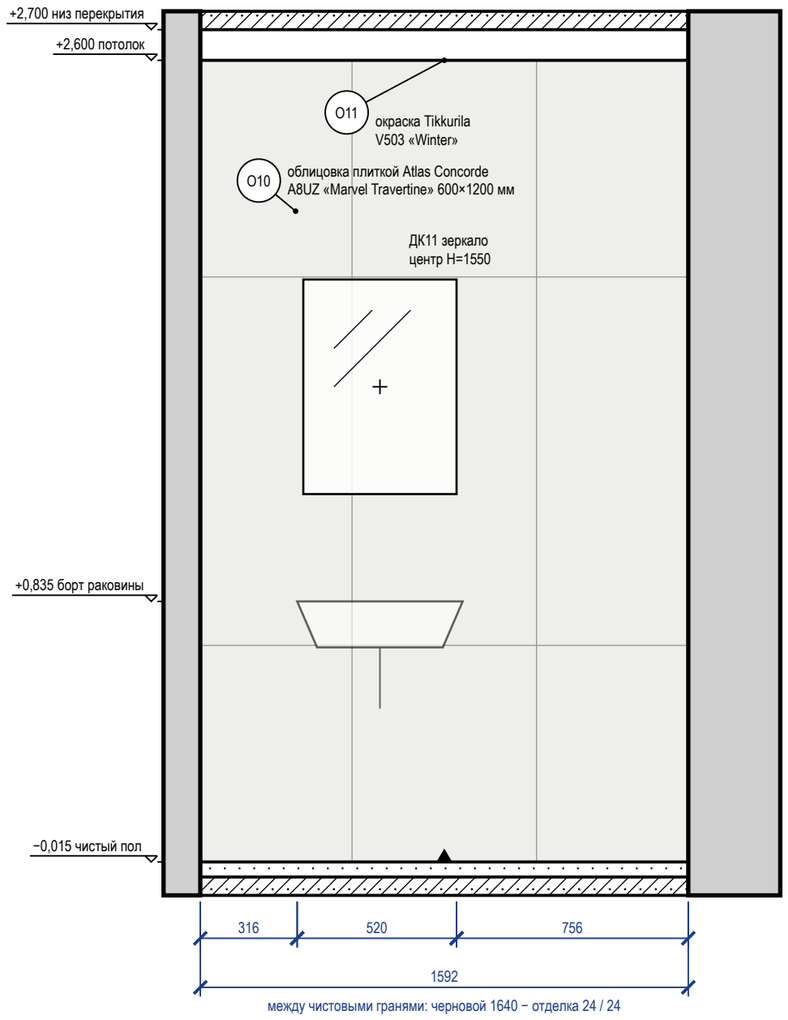

Развёртка стены Б


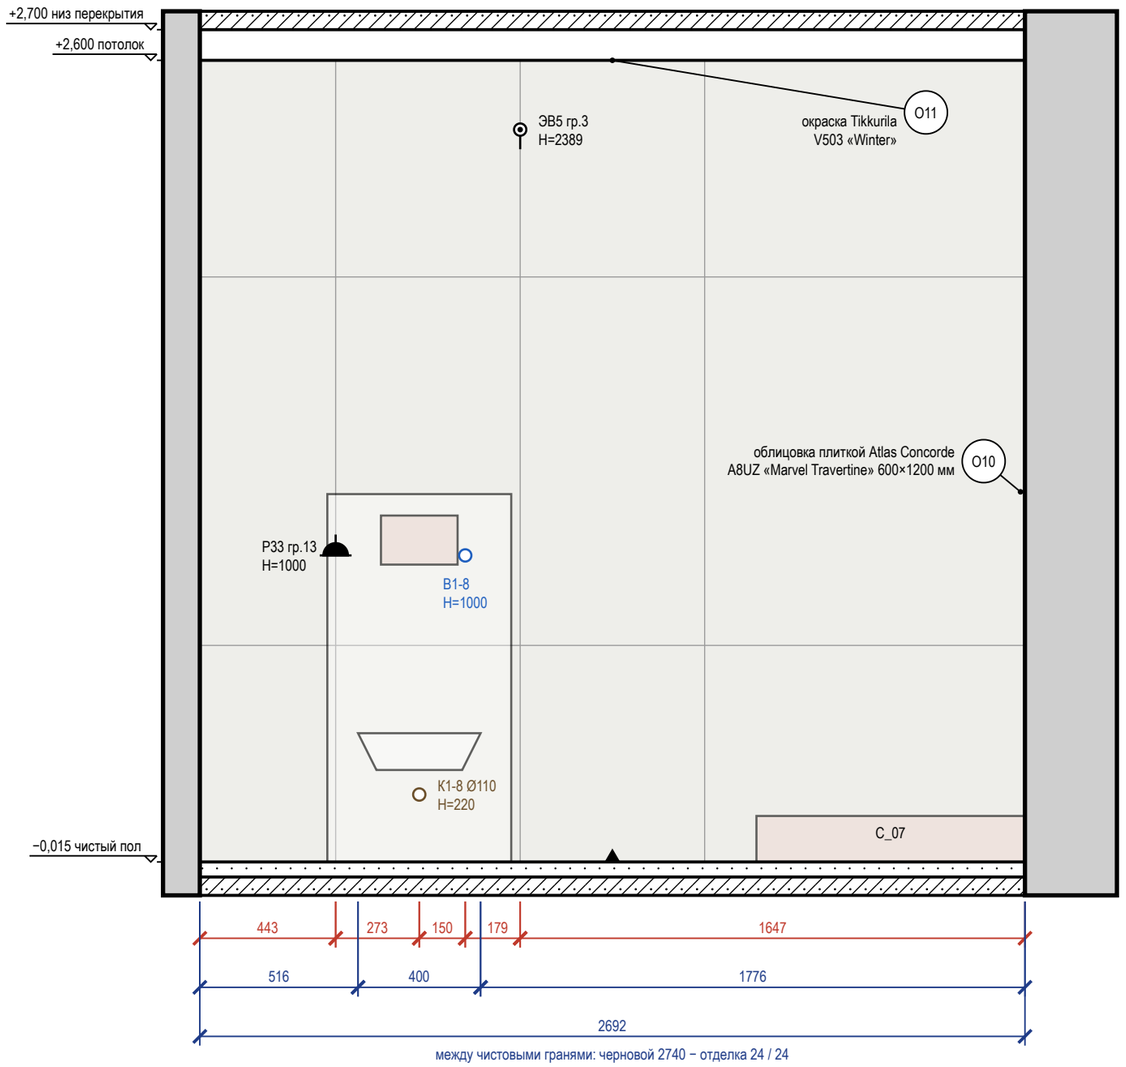


Схема развёрток (М 1:100)

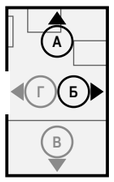

Ведомость отделки (на листе)

Марка	Поверхность	Материал, изделие	Цвет, код	Кол.
О10	стены	облицовка плиткой, Atlas Concorde Marvel Travertine, 600×1200×9 мм, A8UZ, затирка CG2WA	Atlas Concorde A8UZ «Marvel Travertine»	11,2 м²
О11	потолок	окраска, Tikkurila Luja 7, матовая, подготовка Q3	Tikkurila V503 «Winter»	4,5 м²

Визуализация этой стены — лист 26



Примечания

1. Размеры — в мм от чистовых поверхностей стен; условные обозначения и общие указания — лист 27.
2. Стена А показана двумя видами: здесь — архитектурная развёртка (мебель, отделка, проёмы, высоты), электроточки и выводы ВК с привязками и таблицей — на листе 107 («Привязки»).
3. Схема мебели, приборов и декора не является технической документацией для производства мебели; габариты — по паспортам изделий.
4. Облицовка — по сетке швов 2 мм, раскладка от оси стены (треугольник у пола), по высоте — от середины облицовки, подрезки у пола и у потолка поровну; подрезки — по листу раскладки плитки.
5. Гидроизоляция в 2 слоя, заход на стены 200 мм; у душа — на всю высоту стен душевой зоны и 500 мм за край душевой зоны — до облицовки, с актом скрытых работ и тестом проливом (узел — на листе узлов).
6. Картины и зеркала крепить к основанию по паспорту изделия (закладные и анкеры — в перечне скрытых работ); крест — ось центра предмета.

					Проект: Квартира с кабинетом — М 1:20
	Лист	№ док.	Подпись	Дата	
Дизайнер	Кырлан А.С.			04.11.26	Развёртки стен А, Б. Санузел гостевой (пом. 9)

Стадия	Лист	Листов
П	106	127

Развёртка стены А: электроточки и выводы

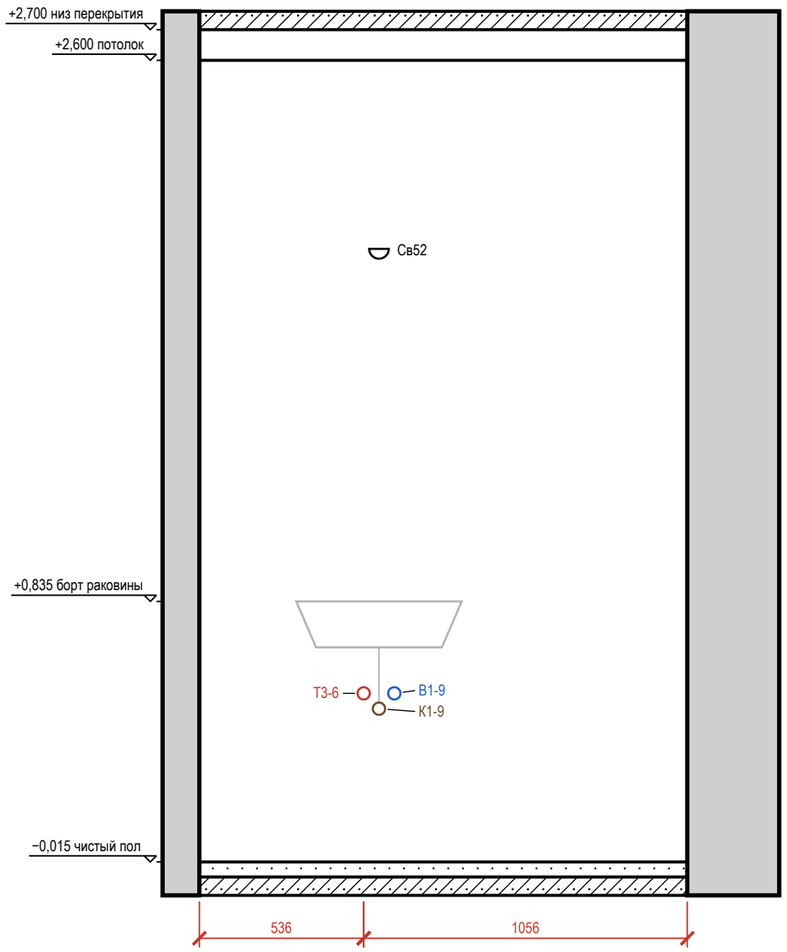



Таблица привязок электроточек и выводов

Марка	Назначение	От угла, мм	Н от пола, мм	Примечание
Т3-6	горячая вода — умывальник	536	550	межос. 100
К1-9	канализация — умывальник	586	500	Ø50
Св52	светильник настенный	586	2000	гр. 3
В1-9	холодная вода — умывальник	636	550	межос. 100

Условные обозначения

- светильник настенный (бра), Н — высота оси
- вывод В1 (код — в ведомости привязок)
- вывод Т3 (код — в ведомости привязок)
- вывод К1 (код — в ведомости привязок)
- привязки точек и выводов от угла и от пола, мм
- марка развёртки: буква стены, стрелка — взгляд

Схема развёрток (М 1:50)

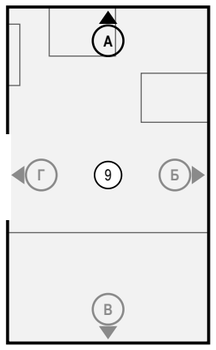


Примечания

1. Вид «Привязки» стены А — электроточки и выводы ВК; архитектурная развёртка (мебель, отделка, проёмы, высоты) — на листе 106. Мебель и приборы — подложкой для ориентира; их марки и обозначения мебели, проёмов и стен — там же.
2. Привязки — в мм: по горизонтали от левого чистового угла стены до оси изделия, Н — от чистого пола до оси; все точки — в таблице привязок. Красная цепочка — привязки по осям; точки ближе 120 мм одна к другой в цепочку не дробятся — их привязки только в таблице.
3. У знака — марка электроточки (Р — розетка, S — выключатель, Св — светильник, ЭВ — вывод кабеля); условные обозначения и общие указания — лист 27.
4. Коды выводов ВК: В1 — холодная вода, Т3 — горячая вода, К1 — канализация; номер после дефиса — номер вывода на листе выводов сантехники.

					Проект: Квартира с кабинетом	М 1:20
	Лист	№ док.	Подпись	Дата	Привязки электроточек и выводов ВК, стена А. Санузел гостевой (пом. 9)	
Дизайнер	Кырлан А.С.			04.11.26		

Стадия	Лист	Листов
П	107	127

Развёртка стены В

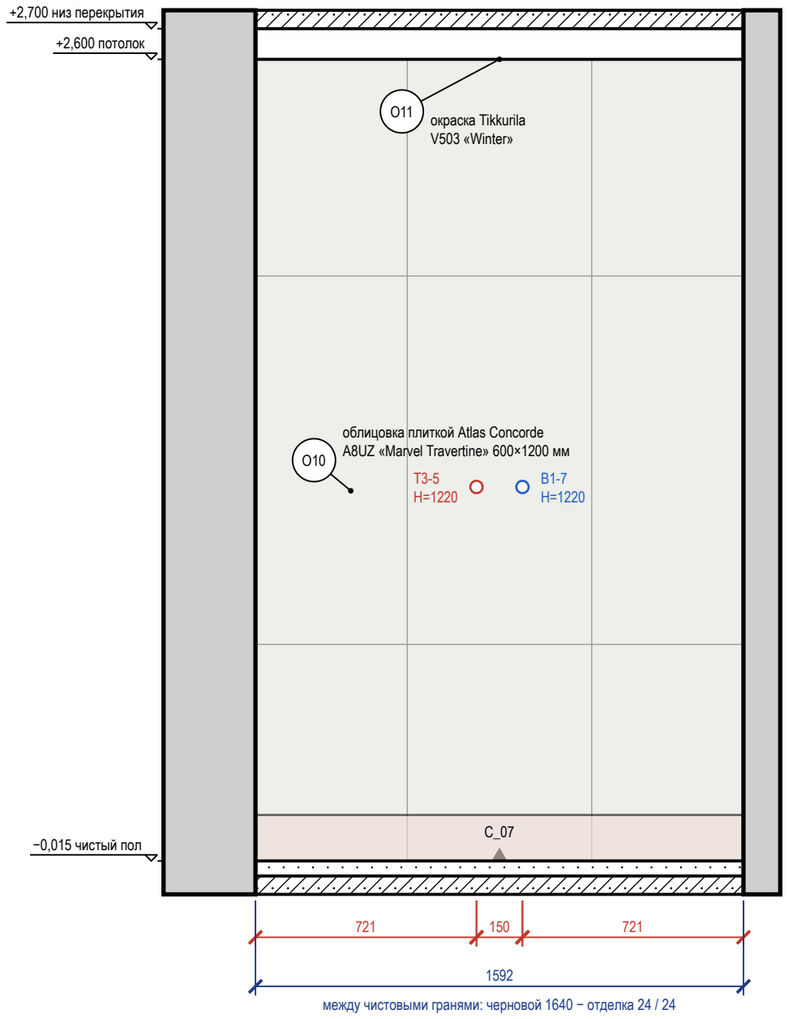

Развёртка стены Г


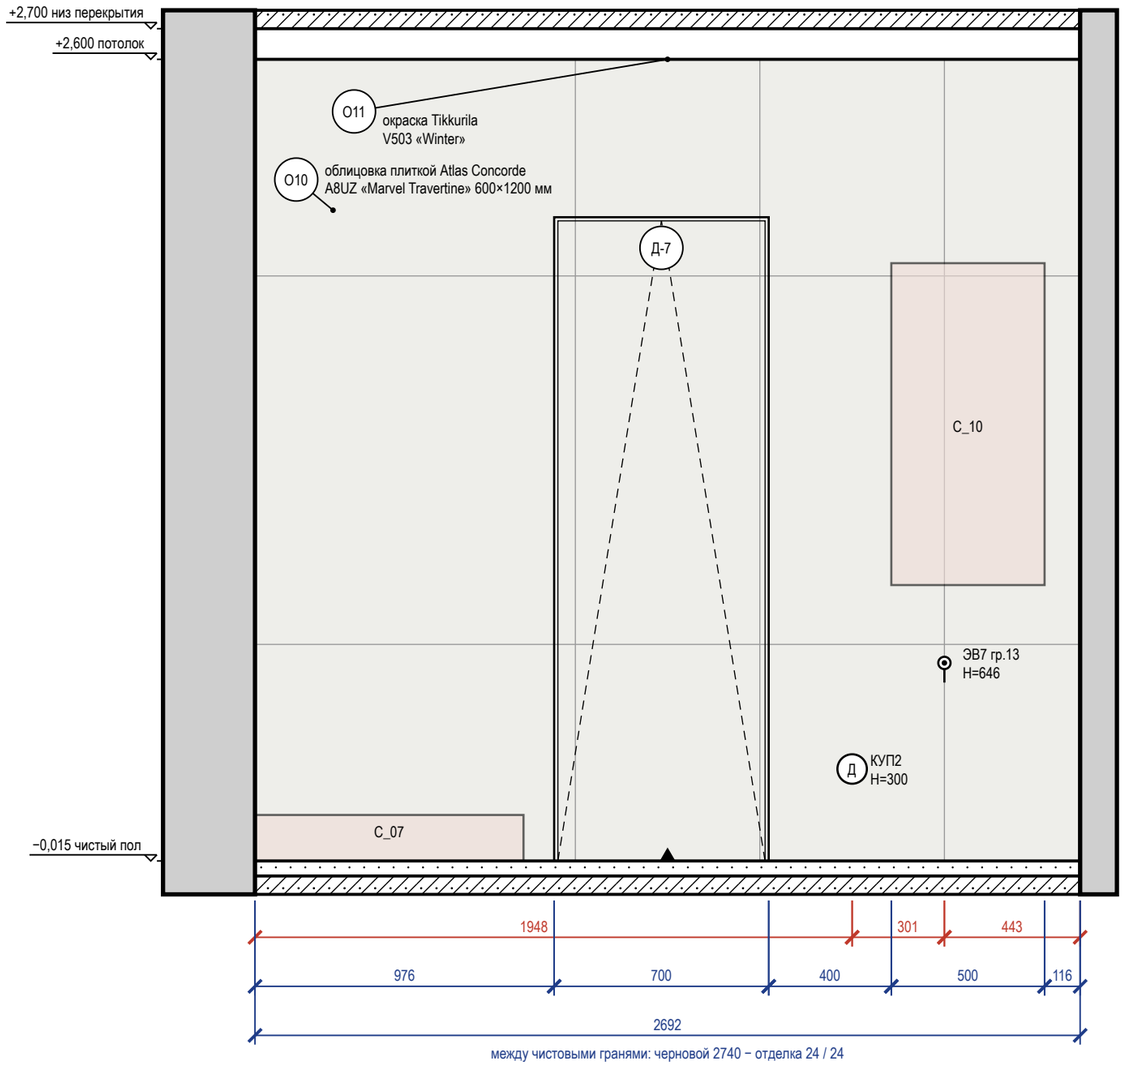


Схема развёрток (М 1:100)

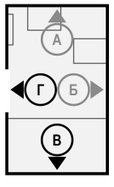

Ведомость отделки (на листе)

Марка	Поверхность	Материал, изделие	Цвет, код	Кол.
О10	стены	облицовка плиткой, Atlas Concorde Marvel Travertine, 600×1200×9 мм, A8UZ, затирка CG2WA	Atlas Concorde A8UZ «Marvel Travertine»	9,7 м²
О11	потолок	окраска, Tikkurila Luja 7, матовая, подготовка Q3	Tikkurila V503 «Winter»	4,5 м²

Визуализация этой стены — лист 25



Примечания

1. Размеры — в мм от чистовых поверхностей стен; условные обозначения и общие указания — лист 27.
2. Схема мебели, приборов и декора не является технической документацией для производства мебели; габариты — по паспортам изделий.
3. Облицовка — по сетке швов 2 мм, раскладка от оси стены (треугольник у пола), по высоте — от середины облицовки, подрезки у пола и у потолка поровну; подрезки — по листу раскладки плитки.
4. Гидроизоляция в 2 слоя, заход на стены 200 мм; у душа — на всю высоту стен душевой зоны и 500 мм за край душевой зоны — до облицовки, с актом скрытых работ и тестом проливом (узел — на листе узлов).
5. Двери скрытого монтажа — полотно в плоскости стены, отделка стены по полотну, плинтус прерывается у короба (узел — на листе узлов).

					Проект: Квартира с кабинетом — М 1:20
	Лист	№ док.	Подпись	Дата	Развёртки стен В, Г. Санузел гостевой (пом. 9)
Дизайнер	Кырлан А.С.			04.11.26	

Стадия	Лист	Листов
П	108	127

выпуск 04.11.2026 № 627e1ac6ce · стр. 108 из 127

Комплект предварительный по пунктам этих таблиц. Пока по пункту нет ответа или решения, показанное на указанном листе — допущение проектировщика, а не утверждённое решение.
Сводка: открытых вопросов — 13 (из них ждут факта объекта — 4: контрольного обмера, обследования или документа); изменений в реестре — 9.

Открытые вопросы и принятые допущения

№	Формулировка	Вид	Кто решает	Если решения нет	Лист, где это проявляется
К-1	Размеры квартиры сняты с растрового плана заказчика с частичными размерами (рисунок не в масштабе): помещения выровнены по подписанным размерам мебели и проходов. До заказа мебели, дверей и материалов нужен контрольный обмер всех помещений и проёмов.	Отсутствует Ждёт: обмера	Архитектор-планировщик	размеры на листах — по плану заказчика, уточняются по месту; мебель на заказ и материалы по ним не заказывать	л. 30 — План планировки от заказчика л. 37 — План размещения мебели и оборудования
К-2	Высота потолка на плане заказчика не указана, принята 2700 мм.	Отсутствует	Архитектор-планировщик	высоты на развёртках и потолки — от 2700 мм, уточнить при обмере	л. 30 — План планировки от заказчика л. 57 — План потолков
К-4	Разрешённая мощность квартиры по ТУ неизвестна, принята 15 кВт.	Отсутствует	Инженер-электрик	щит и группы рассчитаны на 15 кВт; при меньших ТУ пересчёт	л. 63 — Однолинейная схема щита л. 65 — План розеток и электровыводов
К-5	Перепланировка (гардеробная-постирочная при спальне, Г-образный коридор, широкий проём прихожая — гостиная, гостевой санузел у прихожей) — предложение проектировщика: несущие стены дома неизвестны. Нужны поэтажный план БТИ / техзаключение и решение заказчика.	Отсутствует Ждёт: документа	Архитектор-планировщик	перегородки и проёмы — предложение, к строительству не выдаются; мокрые зоны и кухня оставлены на местах плана заказчика	л. 30 — План планировки от заказчика
К-6	Климатический подрайон (СП 131.13330) не задан: принят не северный — жилые комнаты и кухня под потолком от 2,5 м (СП 54, п. 5.12); в IA, IБ, IГ, IД, IVA — от 2,7 м.	Отсутствует Ждёт: документа	Архитектор-планировщик	отметки потолков жилых — по 2,5 м; при северном подрайоне уровни ниже 2,7 м пересчитать до заказа каркаса	л. 57 — План потолков
К-7	Проёмы скрытых дверей Д-2 … Д-7 по плану заказчика высотой 2100 мм, полотно расчётное 2000 мм (ряд UNION FILO-60 Piatto). По каталогам скрытых систем проём под полотно 2000 — 2050–2080 мм, под полотно 2100 — 2150–2180 мм: при проёме 2100 полотно 2000 оставляет над собой лишние 20–50 мм, полотно 2100 не входит. Решить по выбранной модели: проём по высоте 2050–2080 мм под полотно 2000 (как уменьшать — по узлу выбранной модели) или взять полотно 2100 с проёмом 2150–2180 мм (только в ненесущей стене, после контрольного обмера К-1).	Спорно Ждёт: решения	Архитектор-планировщик	проёмы остаются 2100 мм, полотна «расч.» 2000 мм; двери до решения не заказывать	л. 55 — План размещения дверей л. 30 — План планировки от заказчика
К-8	Входная дверь Д-1 (проём 1000 × 2100 мм по плану заказчика): стальной дверной блок не выбран — размер блока и монтажный зазор (ГОСТ 31173-2016) из проёма не выводятся, на листах «блок — задать». Выбрать блок (изготовитель, модель, размер блока, открывание наружу, класс прочности и теплозащиты) и сверить проём по каталогу изготовителя при контрольном обмере (К-1).	Отсутствует Ждёт: решения	Архитектор-планировщик	блок не заказывать, проём не изменять; на листах «блок задать»	л. 55 — План размещения дверей полный альбом
К-10	Душ С_07 с трапом (пом. 9, санузел гостевой, по плану заказчика — «душ с трапом и стеклянной перегородкой»): в стяжке 35 мм с облицовкой 14 мм трап не встаёт — монтажная высота трапа ≈ 90 мм от плиты до верха решётки (по паспорту модели) + уклон отвода Ø50 кратчайшим путём вдоль стен до стояка Ст К1-1 (3,11 м × 25 мм/м = 78 мм) = 168 мм при врезке на уровне плиты; врезка выше плиты поднимает подиум на столько же — отметку врезки замерить (К-1). Предложение проектировщика: душевая зона 900 × 1640 у стены В, подиум 120 мм у трапа (решётка +0,105), ступень по открытому краю 127 мм (уклон 15 мм/м к трапу); гидроизоляция по плите под подиумом и по подиуму, весь санузел; отвод от трапа в подиуме — к стене, за краем подиума — в коробе 160×110 вдоль стены до стояка (узел 1 на схеме разводки); смеситель — 1100 мм от пола душа. Расстановкой не решено: край подиума — в 100 мм от проёма Д-7; не помогает: та же зона глубиной 800 — край в 200 мм; зона 900 × 900 в углу В/Г — край в 100 мм. Решить: (а) зона 900 × 900 в углу В/Б — край в 747 мм от проёма, подиум 110 мм у трапа, ступень 117 мм, отвод 2,74 м; у проёма остаётся пол 740 × 900; кадры визуализации санузла перерисовать; (б) проём Д-7 сдвинуть от зоны (решение архитектора, обмер К-1); (в) оставить зону как есть: ступень у проёма осознанно, кромка ступени контрастная, подсветка у пола. Альтернативы по высоте: низкий поддон на ножках (сифон над полом), сверхплоский трап от 70 мм (подиум 100 мм) или подъём пола всего санузла с порогом.	Спорно Ждёт: обмера, затем решения	Инженер ВК (вода, канализация)	трап и подиум не выполнять, пол санузла 9 до решения не стяжать; гидроизоляцию — по листу	л. 42 — План выводов сантехники л. 43 — Схема разводки водопровода и канализации л. 72 — План покрытий пола
К-11	Ванна С_01 отдельностоящая со смесителем напольным (пом. 7, ванная, по заказчику): подвод ХВ и ГВ к стойке и выпуск Ø50 идут из пола, а стяжка ванной 35 мм их не укрывает — под водопровод Ø20 в полу нужно ≥ 65 мм (Ø + 45, СП 29.13330, п. 8.2), под выпуск Ø50 до стояка Ст К1-2 (3,6 м × 25 мм/м = 90 мм) — ≥ 185 мм. Решить: (а) подъём пола ванной до 185 мм (порог у двери, пересчёт высот выводов и развёрток), (б) смеситель настенный на стене В (выводы ХВ, ГВ на стене) и выпуск ванны к стене открытым сифоном, (в) смеситель на борт ванны. Место стойки на листах — предложение проектировщика.	Спорно Ждёт: решения	Инженер ВК (вода, канализация)	выводы и выпуск ванны С_01 не выполнять, ванну и смеситель не заказывать; остальные выводы ванной — по листу	л. 42 — План выводов сантехники л. 43 — Схема разводки водопровода и канализации л. 52 — Спецификация сантехнического оборудования
К-12	Проверяющий («Пров.») и нормоконтролёр («Н. контр.») комплекта не назначены: графы штампа пусты на всех листах, данные проекта и данные проекта не заданы. Их заполняет только человек, отличный от разработчика: разработчик подписи за них не ставит. Нужно решение автора — кто проверяет и кто ведёт нормоконтроль (фамилии, разные люди), и дата проверки.	Отсутствует Ждёт: решения	Нормоконтролёр	графы «Пров.» и «Н. контр.» остаются пустыми; комплект предварительный, к производству работ не выдаётся	л. 27 — Список листов
К-17	Циркуляция ГВС в данных не задана — циркуляционного трубопровода на схеме нет. Решить: нужна ли циркуляция	Отсутствует Ждёт: решения	Инженер ВК (вода, канализация)	циркуляции на схеме нет	л. 47–50 — Развёртки мокрых зон: выводы ВК. Кухня-гостиная л. 44 — Аксонометрическая схема В1 (холодное водоснабжение) л. 43 — Схема разводки водопровода и канализации

					Проект: Квартира с кабинетом	
	Лист	№ док.	Подпись	Дата	Открытые вопросы, принятые допущения и конфликты. Лист 1 из 3	Стадия / Лист / Листов
Дизайнер	Кырлан А.С.			04.11.26		П / 109 / 127

Открытые вопросы и принятые допущения (продолжение)

№	Формулировка	Вид	Кто решает	Если решения нет	Лист, где это проявляется
К-19	Кухня-гостиная (пом. 4, 45,5 м², два окна): мощность приборов не подтверждена расчётом — РО-5 500×600 (вынесен из модулей, ИЗ-6) и низкий РО-6 1400×200 под банкеткой-экраном (ИЗ-7, теплоотдача за экраном снижается). Нужен теплотехнический расчёт помещения (теплопотери через наружные стены и окна, параметры теплоносителя дома). При нехватке — вертикальный прибор на месте РО-5 или внутрипольный конвектор у окна 2 (решение ОВ).	Отсутствует	Инженер ОВ	РО-5 и РО-6 не заказывать до расчёта; места, подводки и экран — по листам	л. 71 — План отопления
К-20	ТВ-стена М_24: низ ниши ТВ (+900) — в 150 мм над верхом ниши биокамина (+750). Телевизор и приставка на полке над топкой нагреваются; допустимое расстояние задают паспорта обеих моделей (биокамина — зона нагрева над топкой, телевизора температура эксплуатации). Варианты: (а) выбрать модели и подтвердить расстояние по паспортам; (б) поднять нишу ТВ (низ +1100 и выше — центр экрана выше уровня глаз сидящего); (в) развести ниши по ширине стены (камин сбоку от ТВ). Рекомендация исполнителя — (а), при нехватке расстояния — (б).	Спорно Ждёт: решения	Мебельщик	нишу ТВ не изготавливать до выбора моделей; каркас и облицовку вне ниш — по листу	полный альбом л. 92 — Развёртка стены В. Кухня-гостиная (пом. 4)

Изменения проекта после выпуска листов (реестр изменений)

№	Дата	Лист	Было	Стало	Кто решил, подпись
ИЗ-1	26.10.2026	л. 37 — План размещения мебели и оборудования л. 38 — Спецификация мебели и оборудования л. 41 — Ведомости изделий, техники и фурнитуры полный альбом л. 96 — Развёртка стены А. Детская (пом. 6) л. 75 — Развёртка стены А. Спальня (пом. 1)	Шкаф-купе М_30 описан тремя разными изделиями (зеркальные арки / рифлёные панели / ЛДСП); М_08 «с арочными фасадами» без арки на чертеже; кровать детской М_27 на радиаторе РО-9 под окном, ковёр Т22 2500 × 1800 под ней; диван М_22 «угловой» нарисован прямым; у стола М_21 6 стульев, три из них — в банкетке М_20 (за стулом 150 мм). Спальня: шина штор Т1/Т2 одна, 300…2800 по стене А, на окно 1 — пакет штор заходил на окно 2, у окна 2 штор нет.	Предложения проектировщика, заказчиком не утверждены: М_30 — фасад МДФ 10 мм, эмаль матовая, профиль латунь матовая, зеркальные арочные вставки (поле 100 мм), как на кадре; М_08 — арочная фрезеровка филёнок (поле 100 мм); М_27 — кровать 800 × 2000 (было 900 × 2000) у стены Б, 1480 мм от угла с дверью: вне радиатора РО-9, от открытого полотна Д-5 620 мм прохода, вдоль кровати к окну 520 мм (кровать 900 между полотном и стеной В не встаёт: 600 + 900 + 500 > 1940 мм); М_22 — диван угловой Г 2700 × 1600; М_21 — банкетка М_20 на 3 места и 3 стула (2 со свободной стороны, 1 у торца). Т22 — ковёр 1200 × 1700 у кресла-кокона М_28 вместо ковра 2500 × 1800 под кроватью (кровать в 520 мм от стены В: ковёр под ней не выходит за кровать на 450 мм и не оставляет 200 мм пола у стены). До подписи — не заказывать. Знак «**» у М_08 не ставится: марка М_08 совпадает с кодом канализации М_08, и ядро поставило бы знак у каждого «М_08» на листах ВК; предложение по М_08 — только в этой записи. М_27 — изголовье 1000 мм от пола (до выбора модели); ДК2 — низ 1200 мм, на 200 над изголовьем (было 700 от матраса — картина за изголовьем). Спальня: в нише штор по стене А две шины по 2300 мм — Т1/Т2 на окно 1 (0…2300) и Т27/Т28 на окно 2 (2300…4600), верх +2,600 (верх ниши), длину — по обмеру ниши (К-1). Т1, Т2, Т27, Т28 — предложение: на листах со знаком «**», до подписи шины не заказывать.	Утверждено: Кырлан А.С., 01.11.2026. Предложил: исполнитель.
ИЗ-2	30.10.2026	л. 55 — План размещения дверей л. 37 — План размещения мебели и оборудования л. 42 — План выводов сантехники л. 69 — Управление светильниками л. 53 — Раскладка плитки. Ванная. Развёртки стен	Ванная (пом. 7): дверь Д-6 (800 мм, стена А, привязка 2300) открывалась внутрь — полотно на 90° задевало тумбу М_29 (привязка 450) и раковину С_02 (привязка 500): дверь не открыть, в выпуске для заказчика — ошибка; С_02 стояла в полосе 600 мм перед проёмом. Конфликт Кф-3 открыт.	Проём Д-6 сдвинут вдоль стены А от угла Б: привязка 2300 → 1200 (х 4900…5700), петли у х 4900, открывание внутрь, в сторону стены Г (там полотенцесушитель С_06 на стене А 500…1000 — не в секторе). Тумба М_29, раковины С_02, С_03, стиральная машина ОБ_03 остаются на местах; С_02 (500…1100) вне полосы 600 мм перед проёмом. Выключатель S13 в коридоре — к проёму (привязка 3550, со стороны ручки), коробка КУП1 на стене А — привязка 2300. Раскладка плитки стены А пересчитана движком. Знак «**» у Д-6 остаётся до подписи автора; Кф-3 — у владельца до подписи этой записи.	Утверждено: Кырлан А.С., 01.11.2026. Предложил: исполнитель.
ИЗ-3	30.10.2026	л. 37 — План размещения мебели и оборудования полный альбом л. 77 — Привязки электроточек, стена Б. Спальня (пом. 1)	Спальня (пом. 1): кресло-ракушка М_05 (х 600, у 3000, 750×750) перекрывало туалетный столик М_04 (стена В, 500…1700, глубина 450) на 200 мм — на плане кресло поверх столика, на визуализации — рядом; ни одно правило пересечения мебели это не ловило.	М_05 переставлено в угол у окна 1 (х 600…1350, у 600…1350), столик М_04 свободен; кадры спальни сверить с планом заново (views-check). Знак «**» у М_05 до подписи автора.	Утверждено: Кырлан А.С., 01.11.2026. Предложил: исполнитель.
ИЗ-4	30.10.2026	л. 37 — План размещения мебели и оборудования л. 38 — Спецификация мебели и оборудования л. 41 — Ведомости изделий, техники и фурнитуры полный альбом	Марки мебели кабинета К1–К7 совпадали с позициями колерной карты К1–К8, марки прихожей П8, П9 — с сантехприборами П1–П13: марка неоднозначна в пределах комплекта.	Мебель кабинета — М_08, М_09, М_10, М_11, М_12, М_13, ОБ_02, мебель прихожей — М_30 (шкаф-купе), М_31 (банкетка); ссылки точек электрики, текстиля и декора переписаны вместе с марками. Колорист и ВК не тронуты.	Утверждено: Кырлан А.С., 02.11.2026. Предложил: исполнитель.

					Проект: Квартира с кабинетом
	Лист	№ док.	Подпись	Дата	Открытые вопросы, принятые допущения и конфликты. Лист 2 из 3
Дизайнер	Кырлан А.С.			04.11.26	

Стадия	Лист	Листов
П	110	127

Изменения проекта после выпуска листов (реестр изменений) (продолжение)


№	Дата	Лист	Было	Стало	Кто решил, подпись
ИЗ-5	01.11.2026	л. 37 — План размещения мебели и оборудования л. 41 — Ведомости изделий, техники и фурнитуры полный альбом л. 92 — Развёртка стены В. Кухня-гостиная (пом. 4)	ТВ-стена М_24 записана 30.10.2026 «автор: Кырлан А.С.» с нишами ТВ 1500×900 (низ +900) и биокамина 900×400 (низ +350) — размеры задал исполнитель, записи об изменении не было, на листе изделия Д_4 стена рисовалась шкафом с антресолями и штангой.	Предложение исполнителя, заказчиком не утверждено: М_24 — каркас из оцинкованного профиля на стене Б с облицовкой панелями МДФ 19 мм, эмаль; ниша ТВ 1500×900, низ +900, глубина 400, низ ниши — полка под приставку; ниша биокамина 900×400, низ +350 — облицовка негорючая (сталь 2 мм / камень), зазоры 50 мм до панелей — до паспорта модели (К-13). До подписи — не изготавливать.	Утверждено: Кырлан А.С., 01.11.2026. Предложил: предложение исполнителя по наименованию.
ИЗ-6	01.11.2026	л. 71 — План отопления л. Д_9 — Кухня (пом. 4). Развёртка гарнитура л. 89 — Привязки электроточек и выводов ВК, стена А. Кухня-гостиная (пом. 4)	Радиатор РО-5 выводился листом ОВ под окном 1 кухни (стена А, привязка 1050, 700×600) — внутри модулей М_16 (посудомоечная машина) и М_17 (ящики): экран невозможен.	РО-5 — на свободном участке наружной стены А между колонной М_14 и банкеткой М_20: привязка 3350, 500×600, низ +120 (х 11750…12250); гарнитур под окном 1 без прибора. Мощность 500-го прибора сверить теплотехническим расчётом ОВ (при нехватке — вертикальный прибор на том же месте); стояки и подводки отопления не замерены (К-1). Все радиаторы квартиры теперь в данных — одни и те же на листе ОВ, в мебели, DXF и IFC.	Утверждено: Кырлан А.С., 01.11.2026. Предложил: исполнитель (ОВ).
ИЗ-7	01.11.2026	л. 71 — План отопления л. 41 — Ведомости изделий, техники и фурнитуры л. 89 — Привязки электроточек и выводов ВК, стена А. Кухня-гостиная (пом. 4)	Банкетка М_20 у окна 2 — экран радиатора РО-6, выведенного листом ОВ 900×600 (низ +120, верх +720): прибор под сиденье банкетки не вставал, низ щита сиденья не задан.	РО-6 — низкий панельный прибор 1400×200 по ширине окна 2 (привязка 4400, низ +120, верх +320); банкетка М_20: сиденье +450, низ щита сиденья +400 (верх прибора + 80 мм), решётка в лицевой панели, щель 60 мм у стены. Мощность низкого прибора сверить теплотехническим расчётом ОВ (при нехватке — внутрипольный конвектор у окна).	Утверждено: Кырлан А.С., 01.11.2026. Предложил: исполнитель (ОВ, мебель).
ИЗ-8	01.11.2026	полный альбом л. 70 — План вентиляции	Вытяжка над варочной панелью острова М_19 не была задана (К-9); предложение исполнителя — островная потолочная вытяжка в режиме рециркуляции — ждало решения.	Принято автором (ответ передан координатором): островная потолочная вытяжка 900 мм над М_19 в режиме рециркуляции (угольный фильтр), низ +1550. Вариант с отводом в вентканал ВК-3 не выбран: короба в потолке нет. После подписи автора вопрос К-9 закрывается, знак предложения снимается. Модель вытяжки не выбрана: крепление к перекрытию и вывод питания на потолке по паспорту модели.	Утверждено: Кырлан А.С., 01.11.2026. Предложил: Александр Кырлан, решение автора.
ИЗ-9	01.11.2026	л. 37 — План размещения мебели и оборудования л. 41 — Ведомости изделий, техники и фурнитуры полный альбом л. 92 — Развёртка стены В. Кухня-гостиная (пом. 4)	Биокамин в ТВ-стене М_24: модель, мощность, зазоры и приток не заданы (К-13); до ответа нишу камина изготавливать было нельзя.	Принято автором (ответ передан координатором): биокамин в ТВ-стене М_24 остаётся, ниша 900×400, низ +350, облицовка негорючая (сталь 2 мм / камень), зазоры 50 мм до панелей. После подписи автора вопрос К-13 «оставлять ли биокамин» закрывается. Модель биокамина не выбрана: зазоры, тепловая мощность и приток воздуха (при мощности > 2 кВт — решение ОВ) уточняются по паспорту модели — пометка на листе остаётся.	Утверждено: Кырлан А.С., 01.11.2026. Предложил: Александр Кырлан, решение автора.

Примечания


1. Номера листов — по ведомости рабочих чертежей комплекта (лист «Общие данные»).
2. Графа «Если решения нет» показывает состояние решения на листах; влияние на сроки и стоимость по пунктам не оценивалось.
3. Пункт, по которому принято решение, при следующем выпуске комплекта из таблиц исключается.

					Проект: Квартира с кабинетом			
	Лист	№ док.	Подпись	Дата	Открытые вопросы, принятые допущения и конфликты. Лист 3 из 3	Стадия	Лист	Листов
Дизайнер	Кырлан А.С.			04.11.26		П	111	127


Общий вид

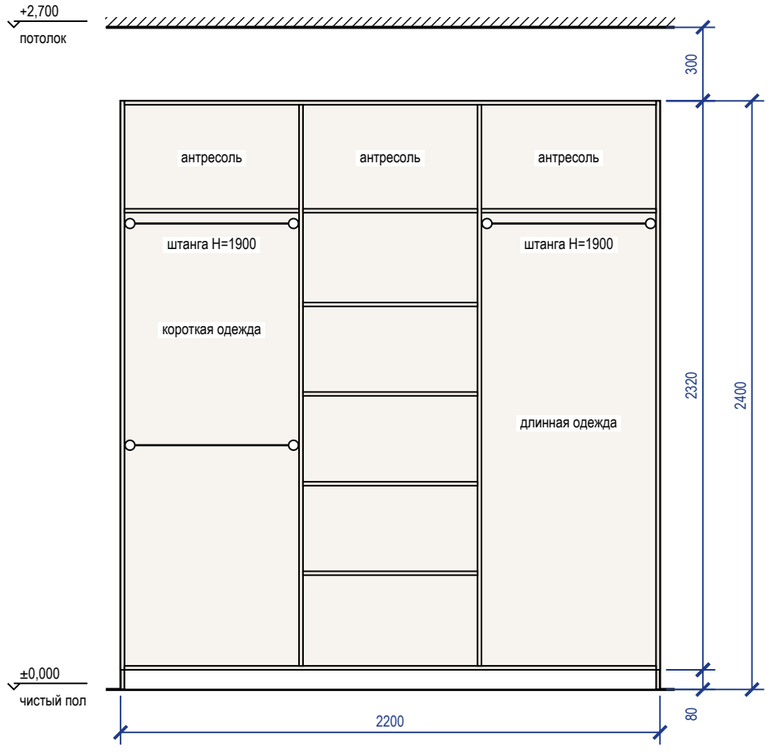


Наполнение, размеры в свету

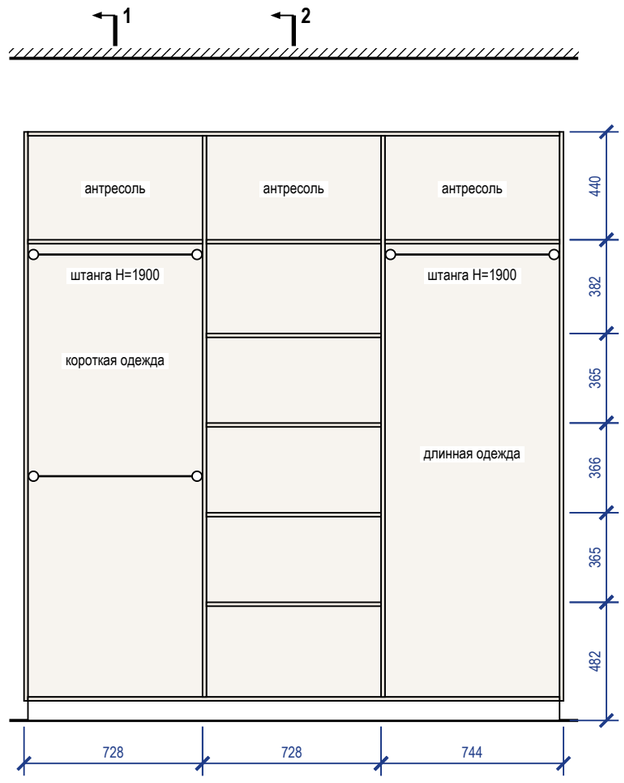

Разрез 1-1

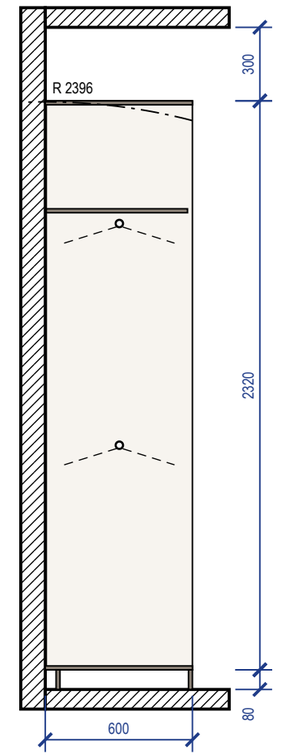


Разрез 2-2

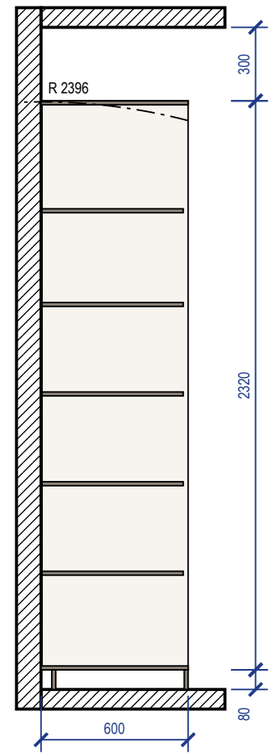

Примечания


1. Размеры — в мм по чистовой отделке; изделие 2200×600×2400 (Ш×Г×В). Перед раскроем — контрольный замер цеха после чистовой отделки стен, пола и потолка.
2. Корпус — ЛДСП 16 мм, задняя стенка ХДФ 4 мм в паз, цоколь 80 мм на регулируемых опорах; открытая система: без фасадов.
3. Кромка: скрытые торцы 0,4 мм, видимые 2 мм (ПВХ/АБС).
4. Присадка по 32-й системе — выполняет цех.
5. Зазор до потолка 300 мм.
6. Подъём корпуса: диагональ боковины без цоколя √(2320² + 600²) = 2396 мм < 2700 мм до потолка — корпус собирается лёжа, поднимается поворотом и ставится на цоколь.
7. Крепление к стене от опрокидывания: крепление к стене, 3 точки; основание стены и шаг анкеров — монтажная схема шкафов.

3D орто

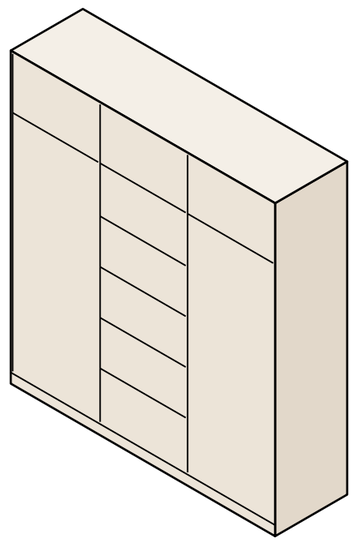


					Проект: Квартира с кабинетом	**М 1:25**
	Лист	№ док.	Подпись	Дата		
Дизайнер	Кырлан А.С.			04.11.26	Система хранения М_06	Стадия: П; Лист: Д_1; Листов: 127


Общий вид

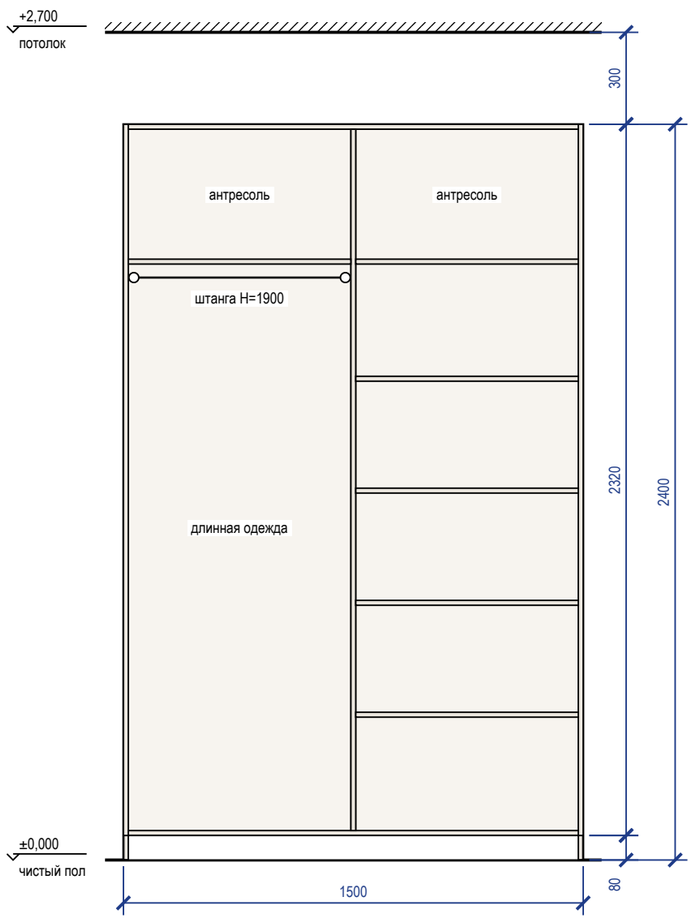


Наполнение, размеры в свету

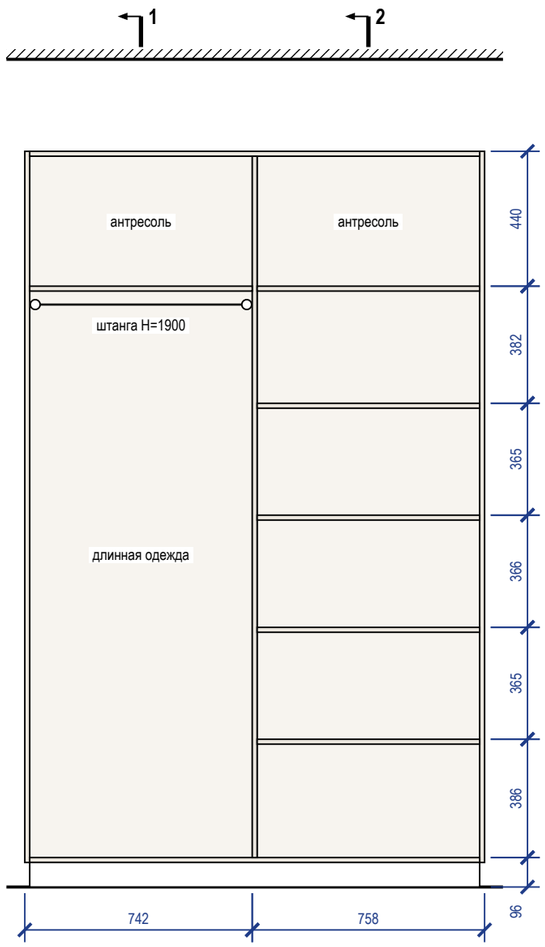

Разрез 1-1

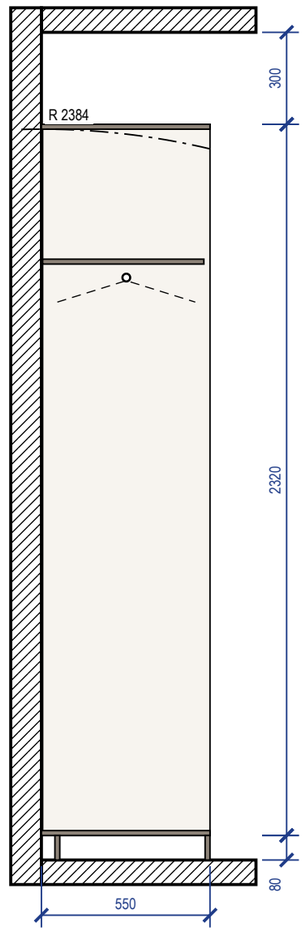


Разрез 2-2

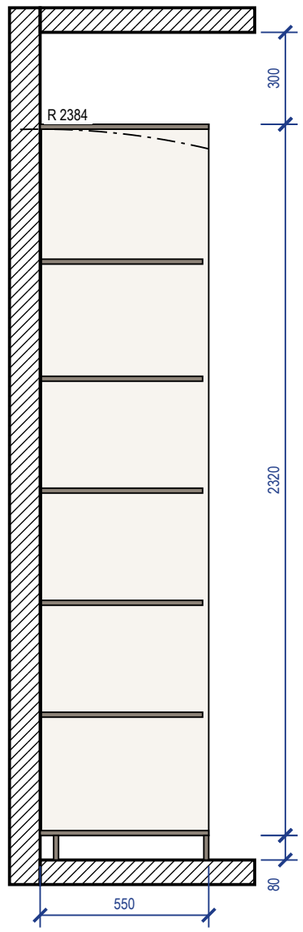

Примечания

1. Размеры — в мм по чистовой отделке; изделие 1500×550×2400 (Ш×Г×В). Перед раскроем — контрольный замер цеха после чистовой отделки стен, пола и потолка.
2. Корпус — ЛДСП 16 мм, задняя стенка ХДФ 4 мм в паз, цоколь 80 мм на регулируемых опорах; открытая система: без фасадов.
3. Кромка: скрытые торцы 0,4 мм, видимые 2 мм (ПВХ/АБС).
4. Присадка по 32-й системе — выполняет цех.
5. Зазор до потолка 300 мм.
6. Подъём корпуса: диагональ боковины без цоколя $\sqrt{(2320^2 + 550^2)} = 2384$ мм < 2700 мм до потолка — корпус собирается лёжа, поднимается поворотом и ставится на цоколь.
7. Крепление к стене от опрокидывания: крепление к стене, 3 точки; основание стены и шаг анкеров — монтажная схема шкафов.


3D орто

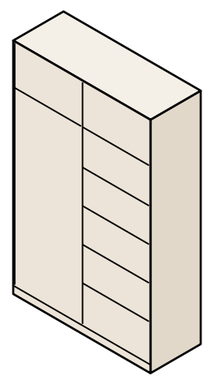


					Проект: Квартира с кабинетом	**М 1:20**
	Лист	№ док.	Подпись	Дата	Система хранения М_07	Стадия / Лист / Листов
Дизайнер	Кырлан А.С.			04.11.26		П / Д_2 / 127

выпуск 04.11.2026 № 627e1ac6ce · стр. 113 из 127


Вид с фасадами

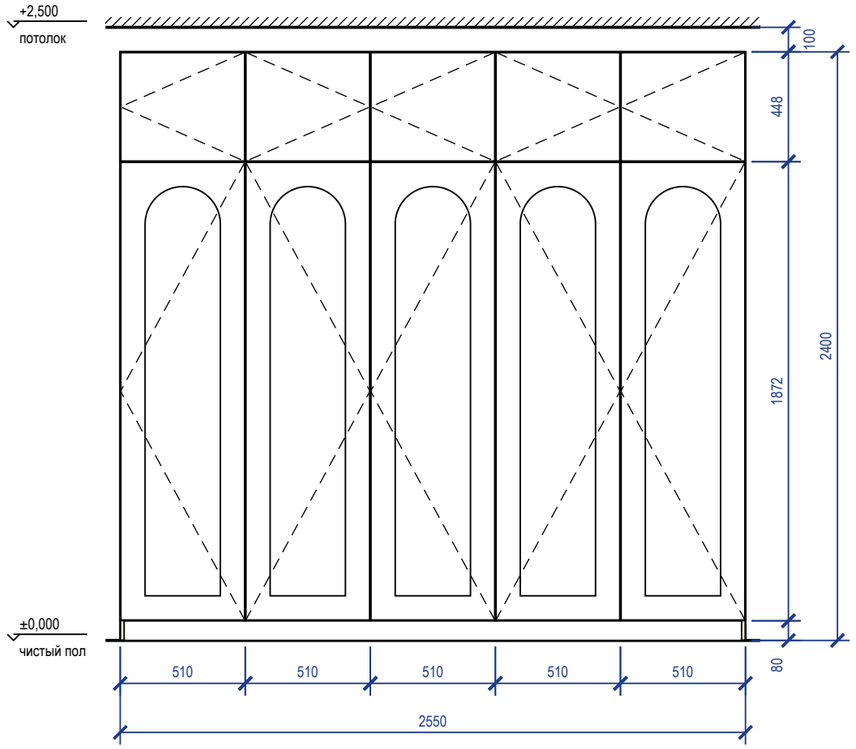


Вид без фасадов

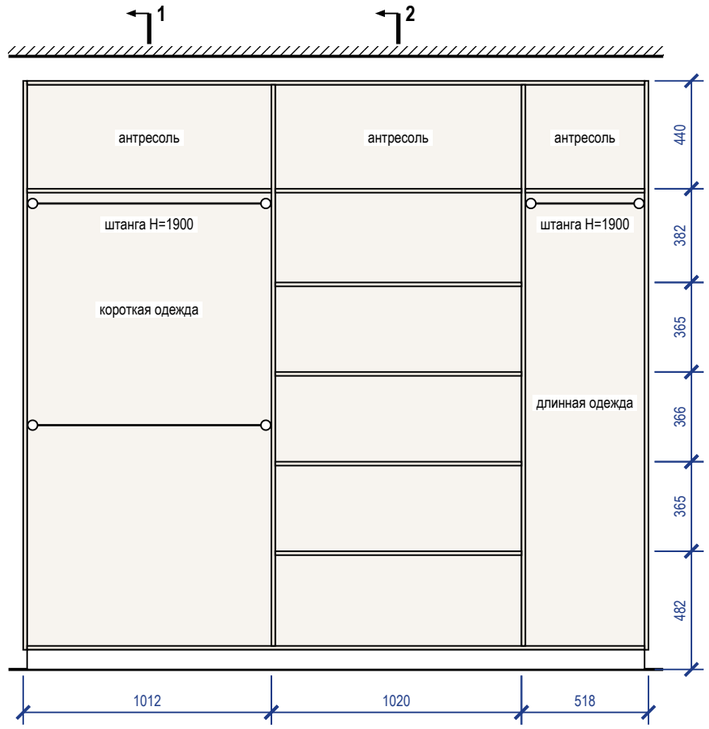

Разрез 1-1

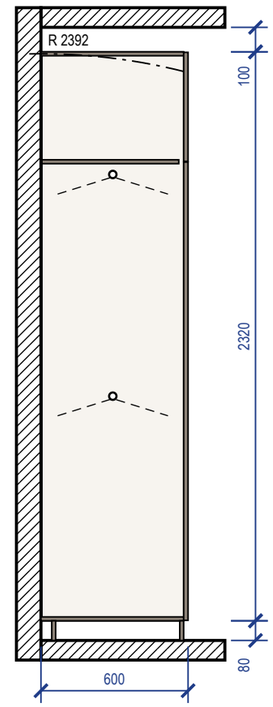


Разрез 2-2

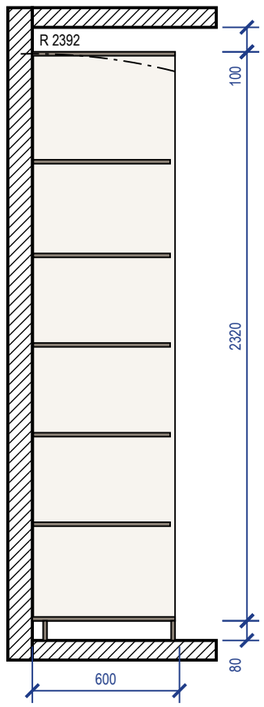

Примечания

1. Размеры — в мм по чистовой отделке; изделие 2550×600×2400 (Ш×Г×В). Перед раскроем — контрольный замер цеха после чистовой отделки стен, пола и потолка.
2. Корпус — ЛДСП 16 мм, задняя стенка ХДФ 4 мм в паз, цоколь 80 мм на регулируемых опорах; фасады накладные — МДФ 18 мм, эмаль матовая; арочная фрезеровка филёнки (полукруглый верх, поле 100 мм); цвет — по колерной карте; петли с доводчиком: фасад 1869 мм — 4 петли, фасад 445 мм — 2 петли.
3. Кромка: скрытые торцы 0,4 мм, видимые 2 мм (ПВХ/АБС).
4. Номинальные зазоры: между фасадами 3 мм, фасад — стена и фасад — потолок не менее 3 мм, фасад ящика — стойка 2 мм.
5. Присадка по 32-й системе — выполняет цех.
6. Зазор до потолка 100 мм — закрыть планкой в цвет корпуса при монтаже.
7. Подъём корпуса: диагональ боковины без цоколя √(2320² + 582²) = 2392 мм < 2500 мм до потолка — корпус собирается лёжа, поднимается поворотом и ставится на цоколь.
8. Крепление к стене от опрокидывания — уголки 2 шт. к несущему основанию (монтажная схема шкафов).


3D орто

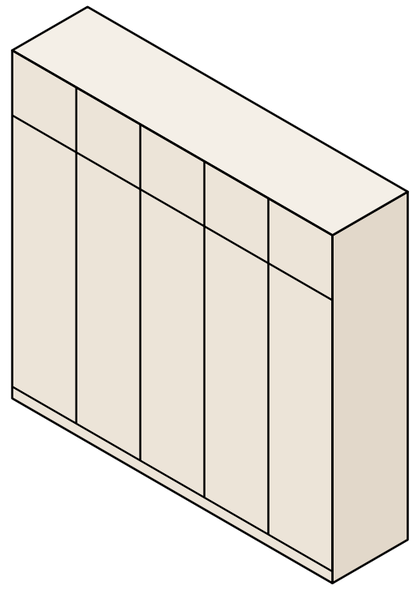


					Проект: Квартира с кабинетом	**М 1:25**
	Лист	№ док.	Подпись	Дата	Шкаф распашной М_08	
Дизайнер	Кырлан А.С.			04.11.26		

Стадия	Лист	Листов
П	Д_3	127


Вид с облицовкой

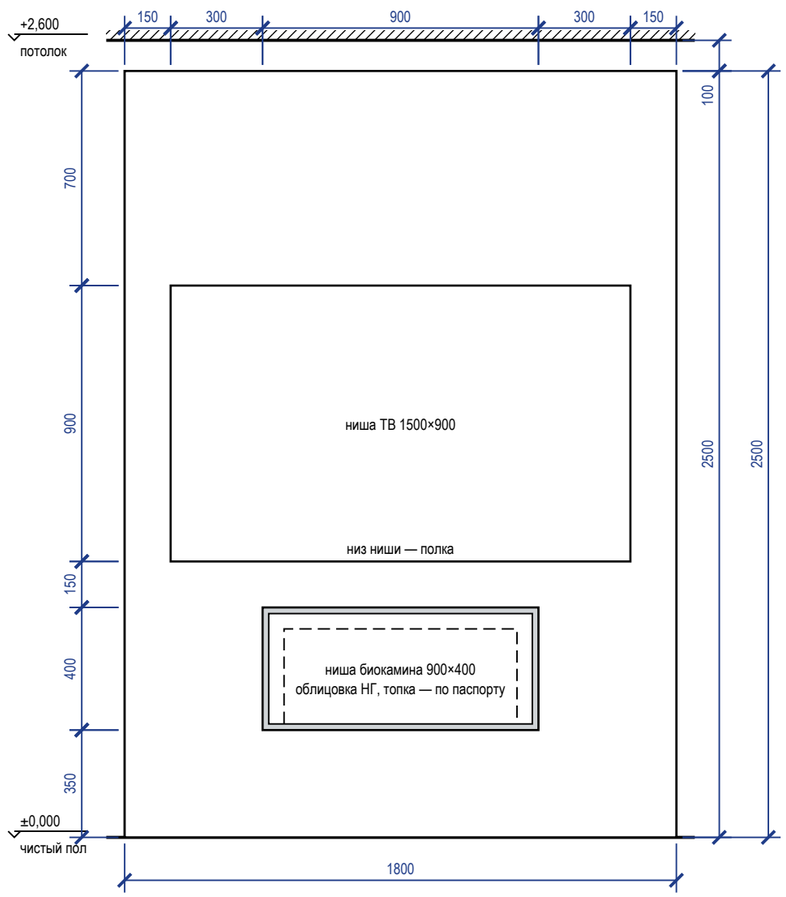

Каркас (без облицовки)

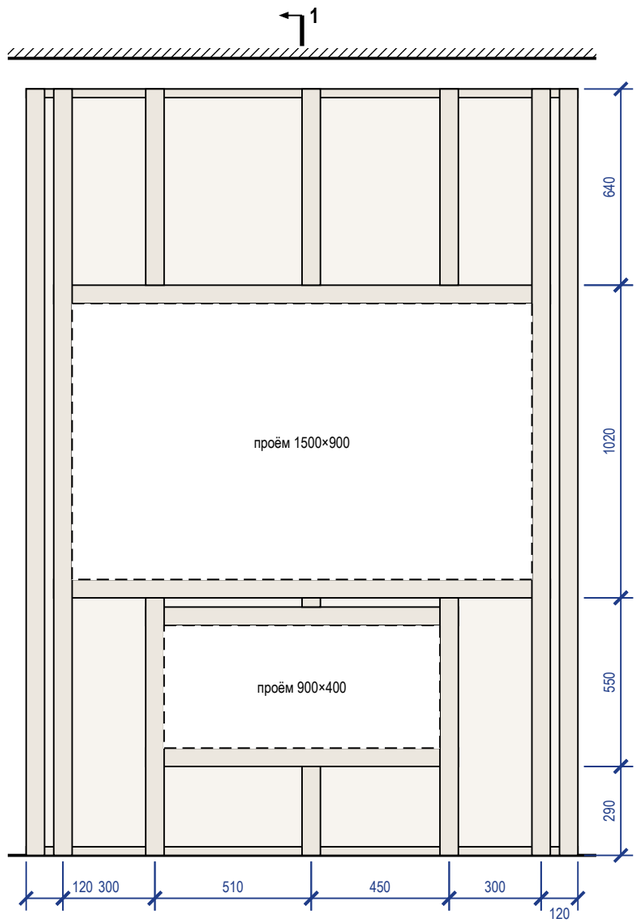


Разрез 1-1 по нишам ТВ и биокамина

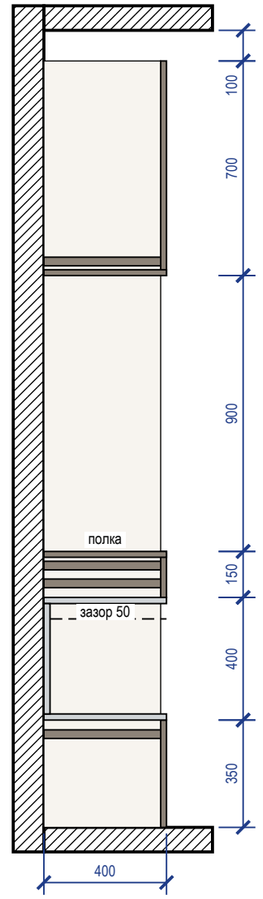

Примечания


1. Размеры — в мм по чистовой отделке; изделие 1800×400×2500 (Ш×Г×В). Встроенная ТВ-стена, не корпусная мебель: отделений, штанг, ящиков и антресолей нет. Перед изготовлением контрольный замер стены после штукатурки и пола.
2. Каркас — оцинкованный профиль ПП 60×27 / ПН 28×27 (НГ), на стене Б; стойки по краям изделия и ниш, промежуточные с шагом не более 600 мм, ригели над и под нишами; облицовка панели МДФ 19 мм с волнистым рельефом, эмаль матовая; цвет — по колерной карте. Собирается на месте у стены, траектории подъёма нет.
3. Ниша ТВ 1500×900, низ +900, глубина 400: низ ниши — полка под приставку, электроточки ТВ-зоны — внутри ниши за телевизором, кабель-канал в каркасе.
4. Ниша биокамина 900×400, низ +350: облицовка — сталь листовая 2 мм / камень натуральный, негорючие (НГ, ГОСТ 30244), 20 мм; зазоры до топки над ней 50 мм, по бокам 50 мм — до выбора модели; окончательно — по паспорту биокамина. Каркас вокруг ниши — металлический профиль (НГ), ЛДСП, МДФ и дерево в нише и в зазорах не применять.
5. ТВ над топкой: от верха ниши биокамина (+750) до низа ниши ТВ (+900) — 150 мм; нагрев телевизора и приставки над топкой — расстояние по паспортам обеих моделей; до выбора моделей нишу ТВ не изготавливать.
6. Крепление к стене: стойки и направляющие — анкерами к основанию стены; основание стены и шаг анкеров — монтажная схема.

3D орто

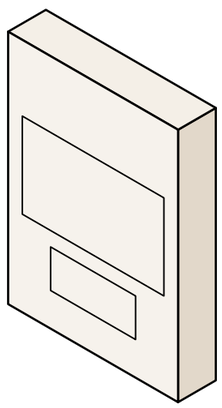


					Проект: Квартира с кабинетом	М 1:20
	Лист	№ док.	Подпись	Дата		
Дизайнер	Кырлан А.С.			04.11.26	ТВ-стена M_24	Стадия: П; Лист: Д_4; Листов: 127


Вид с фасадами

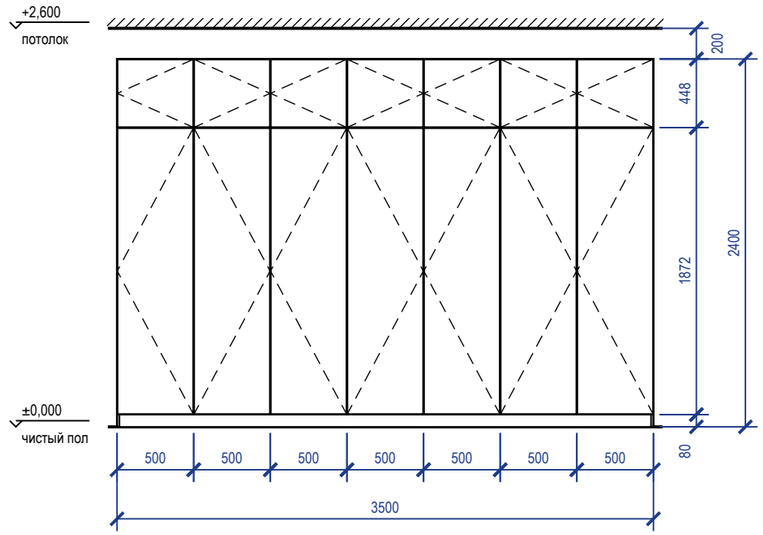


Вид без фасадов

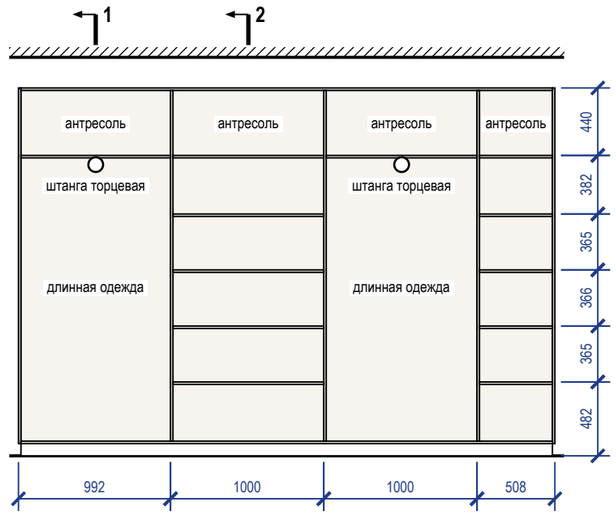

Разрез 1-1

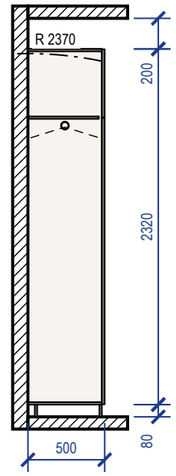

Разрез 2-2

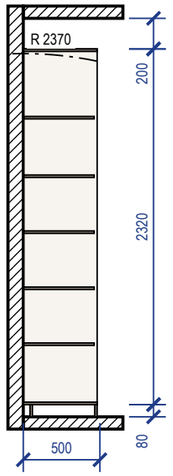


Примечания

1. Размеры — в мм по чистовой отделке; изделие 3500×500×2400 (Ш×Г×В). Перед раскроем — контрольный замер цеха после чистовой отделки стен, пола и потолка.
2. Корпус — ЛДСП 16 мм, задняя стенка ХДФ 4 мм в паз, цоколь 80 мм на регулируемых опорах; фасады накладные — МДФ 18 мм, эмаль матовая, 18 мм; цвет — по колерной карте; петли с доводчиком: фасад 1869 мм — 4 петли, фасад 445 мм — 2 петли.
3. Кромка: скрытые торцы 0,4 мм, видимые 2 мм (ПВХ/АБС).
4. Номинальные зазоры: между фасадами 3 мм, фасад — стена и фасад — потолок не менее 3 мм, фасад ящика — стойка 2 мм.
5. Присадка по 32-й системе — выполняет цех.
6. Зазор до потолка 200 мм.
7. Подъём корпуса: диагональ боковины без цоколя √(2320² + 482²) = 2370 мм < 2600 мм до потолка — корпус собирается лёжа, поднимается поворотом и ставится на цоколь.
8. Крепление к стене от опрокидывания — уголки 2 шт. к несущему основанию (монтажная схема шкафов).


3D орто

					Проект: Квартира с кабинетом	**М 1:40**
	Лист	№ док.	Подпись	Дата		
Дизайнер	Кырлан А.С.			04.11.26	Шкаф распашной М_25	Стадия: П; Лист: Д_5; Листов: 127


Вид с фасадами

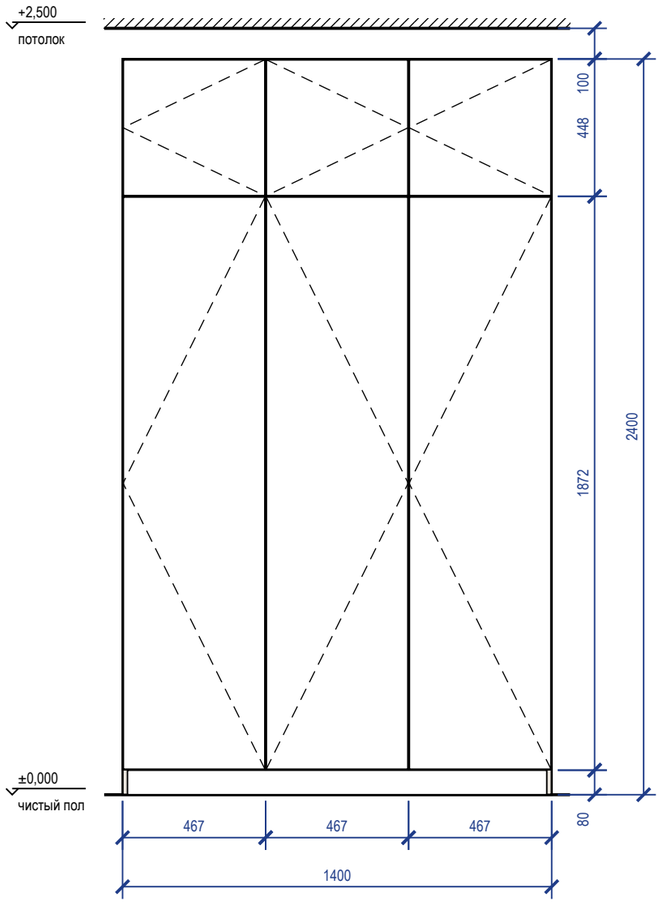


Вид без фасадов

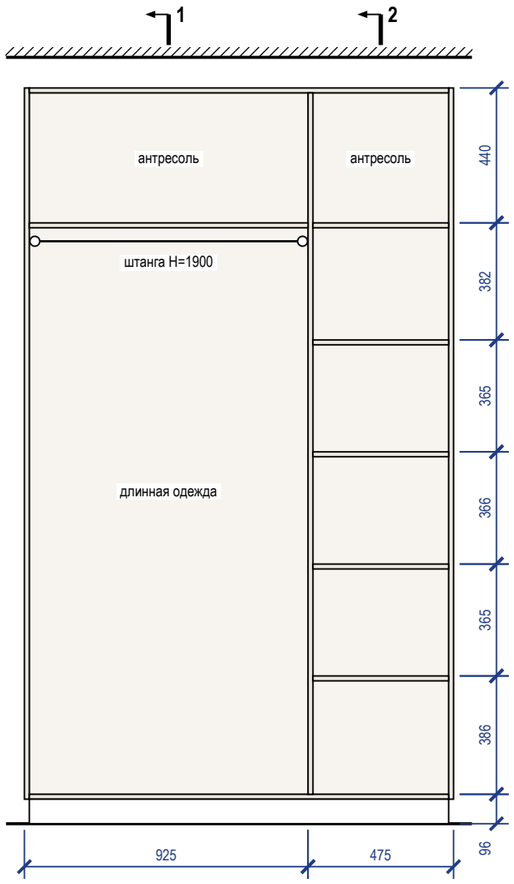

Разрез 1-1

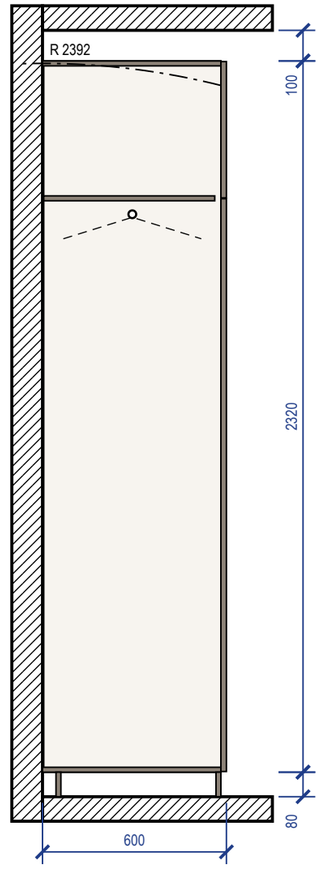


Разрез 2-2

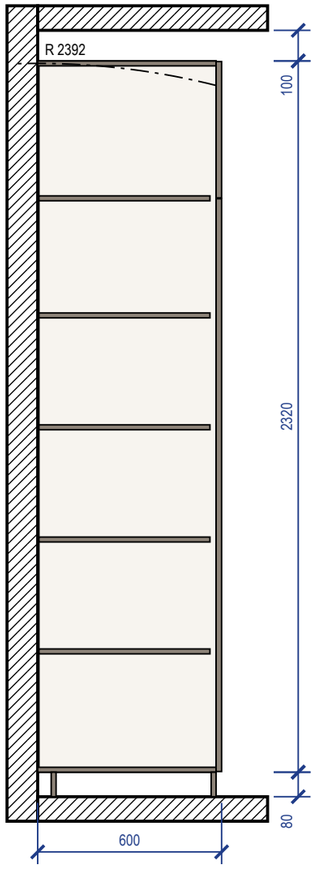

Примечания


1. Размеры — в мм по чистовой отделке; изделие 1400×600×2400 (Ш×Г×В). Перед раскроем — контрольный замер цеха после чистовой отделки стен, пола и потолка.
2. Корпус — ЛДСП 16 мм, задняя стенка ХДФ 4 мм в паз, цоколь 80 мм на регулируемых опорах; фасады накладные — МДФ 18 мм, эмаль матовая, 18 мм; цвет — по колерной карте; петли с доводчиком: фасад 1869 мм — 4 петли, фасад 445 мм — 2 петли.
3. Кромка: скрытые торцы 0,4 мм, видимые 2 мм (ПВХ/АБС).
4. Номинальные зазоры: между фасадами 3 мм, фасад — стена и фасад — потолок не менее 3 мм, фасад ящика — стойка 2 мм.
5. Присадка по 32-й системе — выполняет цех.
6. Зазор до потолка 100 мм — закрыть планкой в цвет корпуса при монтаже.
7. Подъём корпуса: диагональ боковины без цоколя $\sqrt{(2320^2 + 582^2)} = 2392$ мм < 2500 мм до потолка — корпус собирается лёжа, поднимается поворотом и ставится на цоколь.
8. Крепление к стене от опрокидывания: крепление к стене, 2 точки; основание стены и шаг анкеров — монтажная схема шкафов.

3D орто

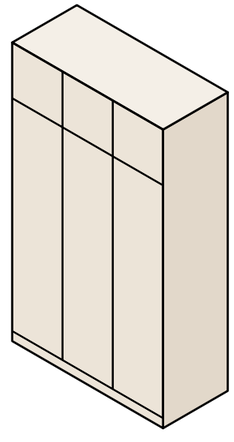


					Проект: Квартира с кабинетом	**М 1:20**
	Лист	№ док.	Подпись	Дата		
Дизайнер	Кырлан А.С.			04.11.26	Шкаф распашной М_26	Стадия: П; Лист: Д_6; Листов: 127


Вид с фасадами

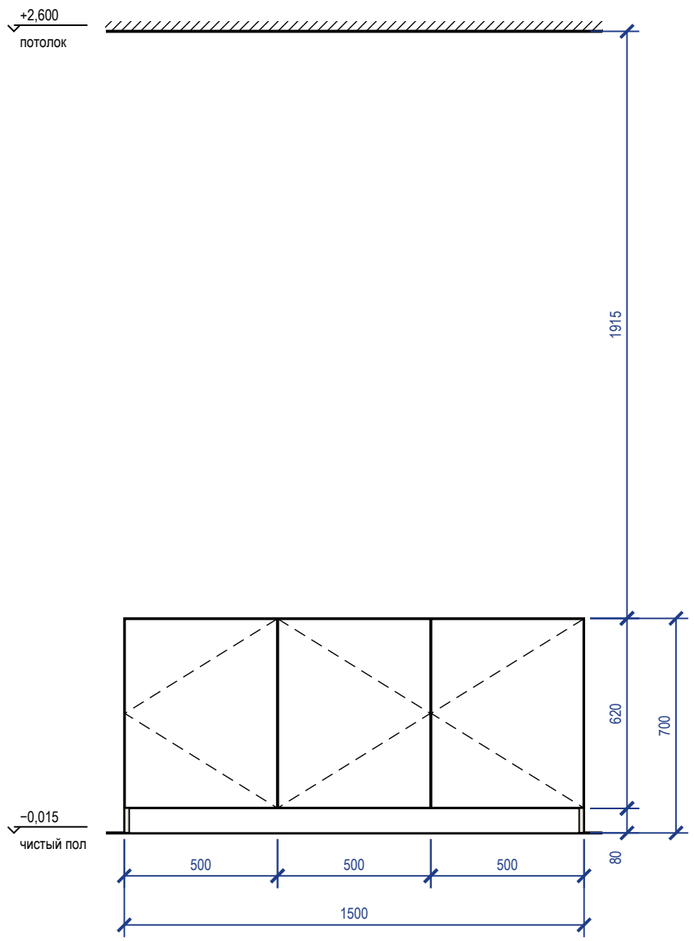

Вид без фасадов

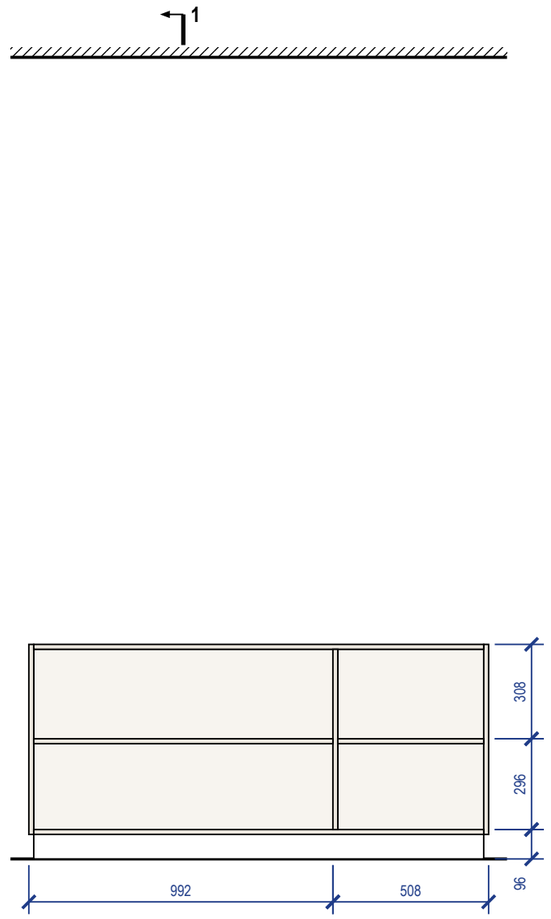


Разрез 1-1

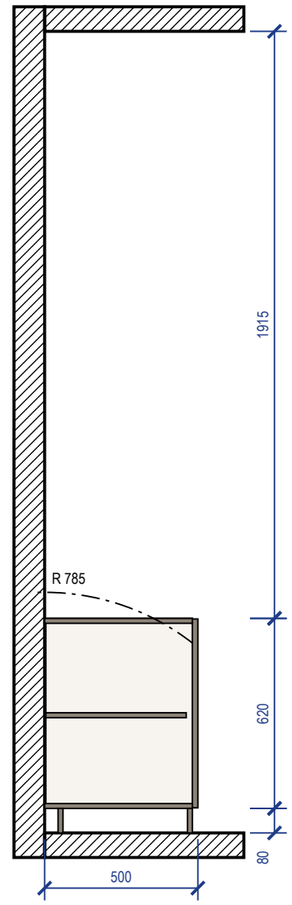

Примечания


1. Размеры — в мм по чистовой отделке; изделие 1500×500×700 (Ш×Г×В). Перед раскроем — контрольный замер цеха после чистовой отделки стен, пола и потолка.
2. Корпус — ЛДСП 16 мм, задняя стенка ХДФ 4 мм в паз, цоколь 80 мм на регулируемых опорах; фасады накладные — МДФ 18 мм, эмаль матовая, 18 мм; цвет — по колерной карте; петли с доводчиком: фасад 616 мм — 2 петли.
3. Кромка: скрытые торцы 0,4 мм, видимые 2 мм (ПВХ/АБС).
4. Номинальные зазоры: между фасадами 3 мм, фасад — стена и фасад — потолок не менее 3 мм, фасад ящика — стойка 2 мм.
5. Присадка по 32-й системе — выполняет цех.
6. Зазор до потолка 1915 мм.
7. Подъём корпуса: диагональ боковины без цоколя √(620² + 482²) = 785 мм < 2615 мм до потолка — корпус собирается лёжа, поднимается поворотом и ставится на цоколь.
8. Крепление к стене от опрокидывания: крепление к стене, 2 точки; основание стены и шаг анкеров — монтажная схема шкафов.

3D орто

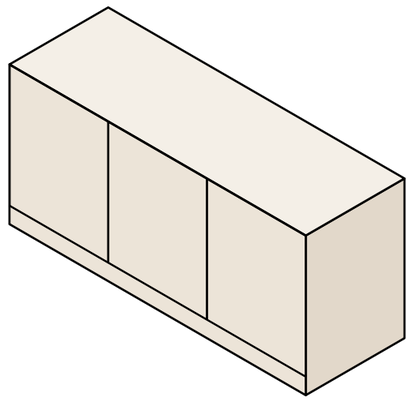


					Проект: Квартира с кабинетом	**М 1:20**
	Лист	№ док.	Подпись	Дата	Тумба под раковину М_29	Стадия / Лист / Листов
Дизайнер	Кырлан А.С.			04.11.26		П / Д_7 / 127


Вид с фасадами

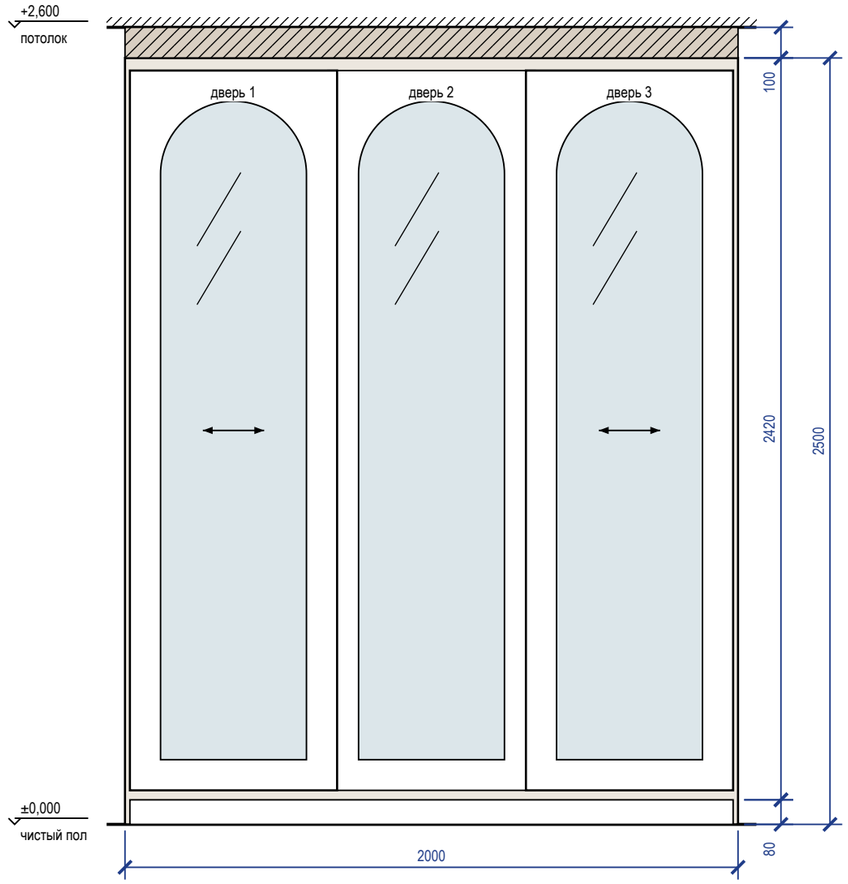


Вид без фасадов

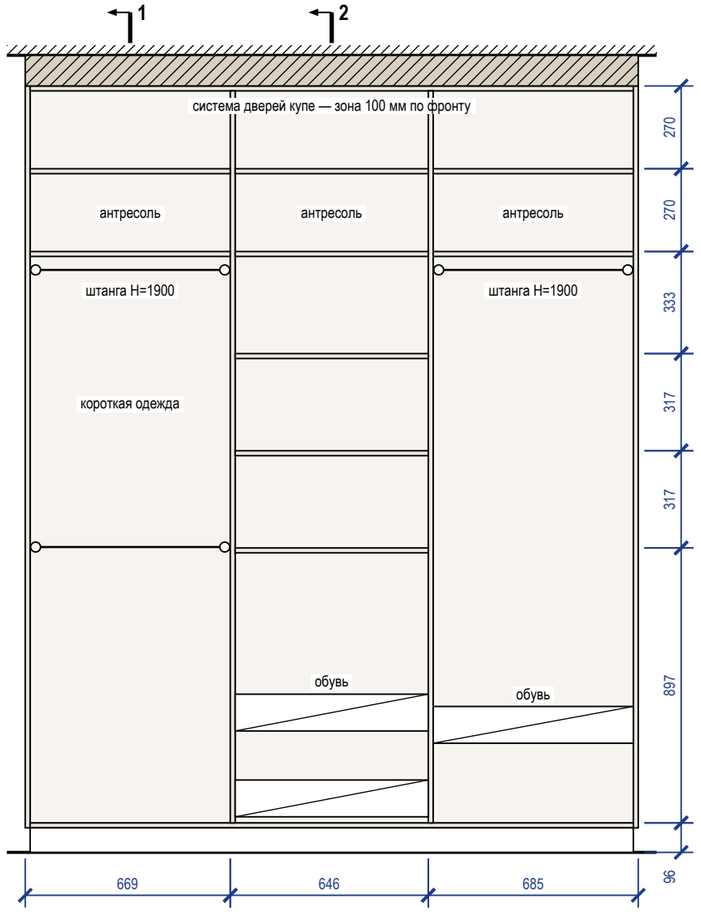

Разрез 1-1

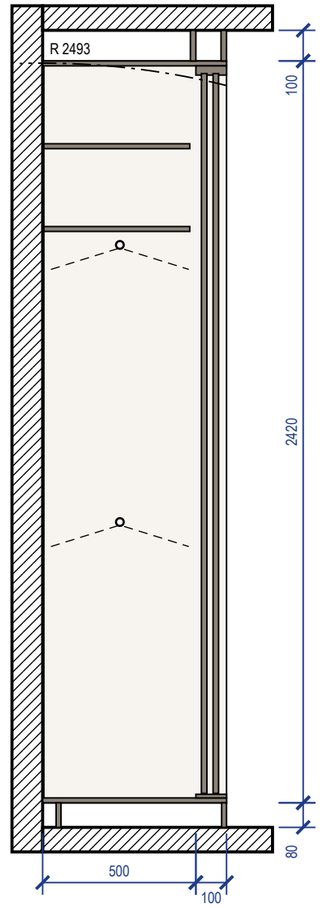


Разрез 2-2

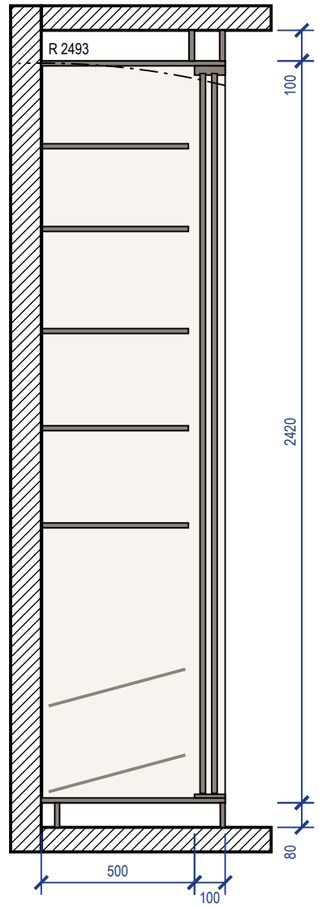

Примечания

1. Размеры — в мм по чистовой отделке; изделие 2000×600×2500 (Ш×Г×В). Перед раскроем — контрольный замер цеха после чистовой отделки стен, пола и потолка.
2. Корпус — ЛДСП 16 мм, задняя стенка ХДФ 4 мм в паз, цоколь 80 мм на регулируемых опорах; двери купе — МДФ 10 мм, эмаль матовая в профиле: алюминий, латунь матовая; вставка зеркало серебро 4 мм, плёнка безопасности, арочная (полукруглый верх, поле 100 мм); нахлёст 30 мм, ширина двери 676 мм, высота — проём минус 40 мм; цвет — по колерной карте.
3. Кромка: скрытые торцы 0,4 мм, видимые 2 мм (ПВХ/АБС).
4. Номинальные зазоры: дверь купе — боковина 3 мм, фасад ящика — стойка 2 мм; ящики внутри купе — с накладкой 30 мм на стойке со стороны нахлёста дверей.
5. Присадка по 32-й системе — выполняет цех.
6. Компенсатор 100 мм — короб из ЛДСП по фронту и торцам, подгоняется к потолку при монтаже (припуск 20 мм), крепится к корпусу и к потолку.
7. Подъём корпуса: диагональ боковины без цоколя $\sqrt{(2420^2 + 600^2)} = 2493$ мм < 2600 мм до потолка — корпус собирается лёжа, поднимается поворотом и ставится на цоколь.
8. Крепление к стене от опрокидывания — уголки 2 шт. к несущему основанию (монтажная схема шкафов).


3D орто

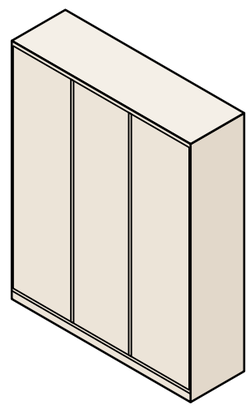


					Проект: Квартира с кабинетом		**M 1:20**
	Лист	№ док.	Подпись	Дата	Шкаф-купе M_30	Стадия	Лист	Листов
Дизайнер	Кырлан А.С.			04.11.26		П	Д_8	127

выпуск 04.11.2026 № 627e1ac6ce · стр. 119 из 127


Вид с фасадами

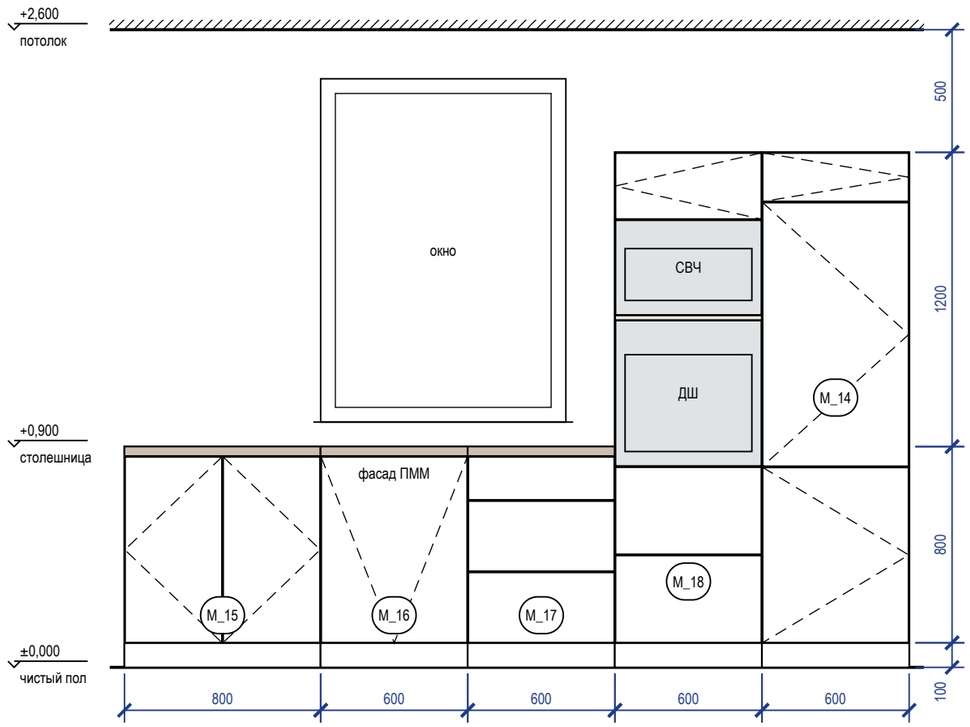


Вид без фасадов (наполнение, выводы)

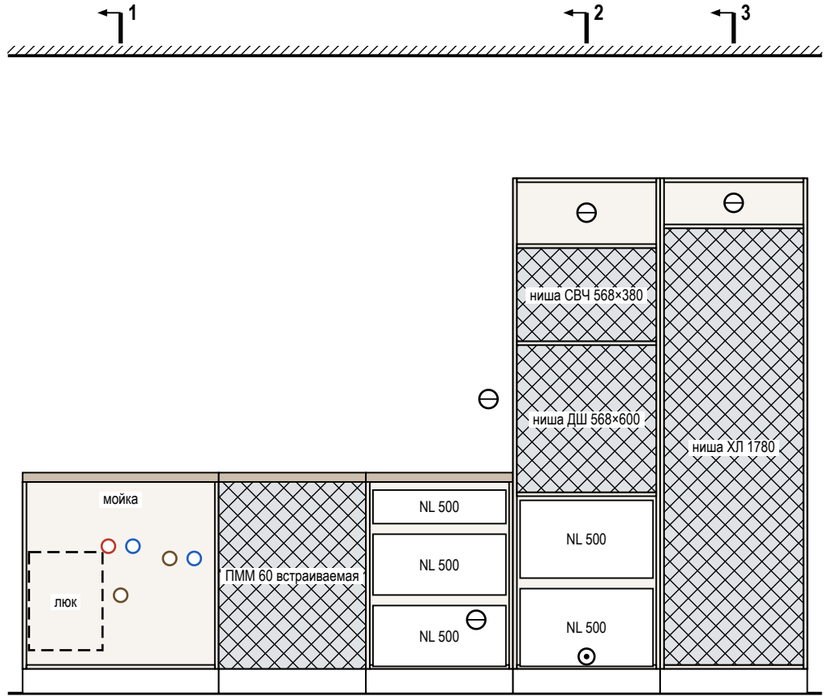


Разрез 1-1

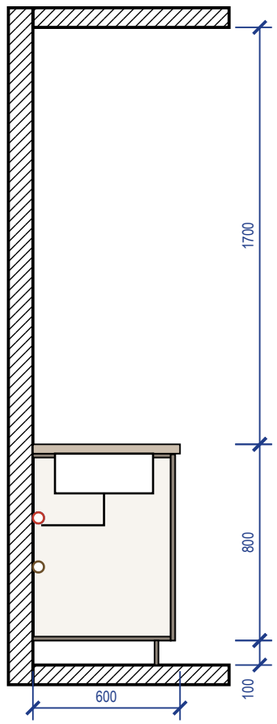


Разрез 2-2

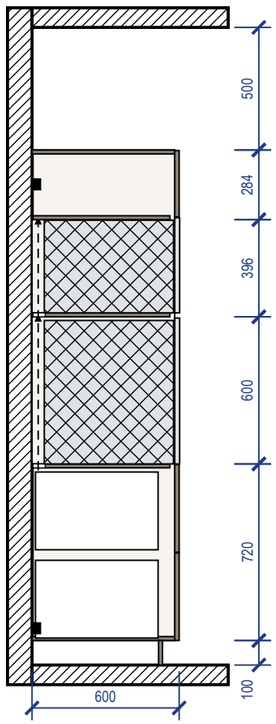

Разрез 3-3

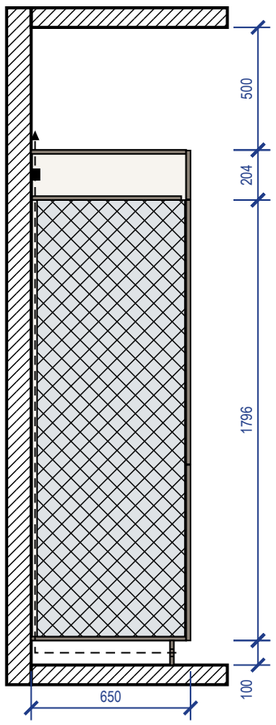

3D орто

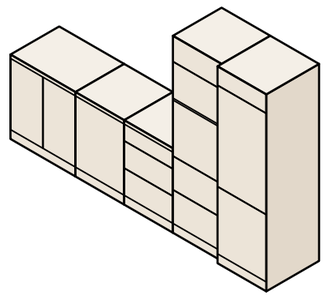


Примечания

1. Размеры — в мм по чистовой отделке, вид из помещения; марки — как на плане расстановки. Перед раскроем — контрольный замер цеха после фартука и пола.
2. Корпуса — ЛДСП 16 мм, задняя стенка ХДФ 4 мм; фасады — МДФ, эмаль матовая 18 мм, цвет по колерной карте; столешница 38 мм, свес 20 мм; цоколь 100 мм.
3. Кромка: скрытые торцы 0,4 мм, видимые 2 мм. Номинальные зазоры: между фасадами 3 мм, фасад — столешница 3 мм, фасад — стена не менее 3 мм.
4. Ящики полного выдвижения и петли — с доводчиком; присадка по 32-й системе — выполняет цех.
5. Ниши техники (холодильник — ориентир 1780 мм) — по монтажным схемам выбранных моделей: решётка в цоколе и канал за пеналом холодильника, зазор за духовым шкафом, фасад ПММ на двери машины.
6. Вентиляция: задняя стенка в зоне ниш не ставится, зазор 50 мм до стены, щель 50 мм в полке под каждой нишей у задней стенки.
7. М_15: сервисный люк к стоякам Ст К1-3 (кухня), Ст В1-3 — съёмная панель 300×400 мм в задней стенке на саморезах (по виду без фасадов, штриховой контур «люк»), доступ через фасад модуля; короб стояков за модулем — с ревизией напротив люка (лист ВК).


					Проект: Квартира с кабинетом	М 1:25
	Лист	№ док.	Подпись	Дата	Кухня (пом. 4). Развёртка гарнитура	Стадия / Лист / Листов
Дизайнер	Кырлан А.С.			04.11.26		П / Д_9 / 127

План (вид сверху)

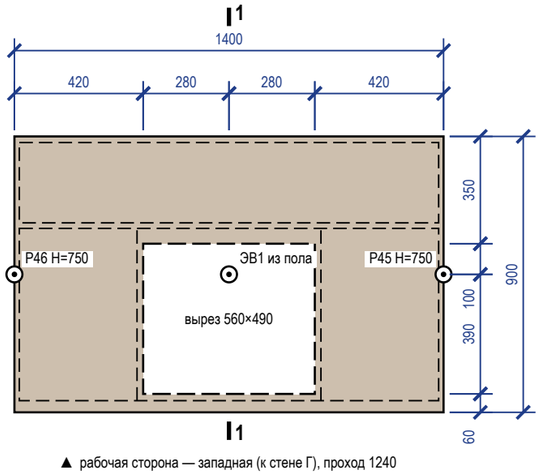


▲ рабочая сторона — западная (к стене Г), проход 1240


Вид с рабочей стороны

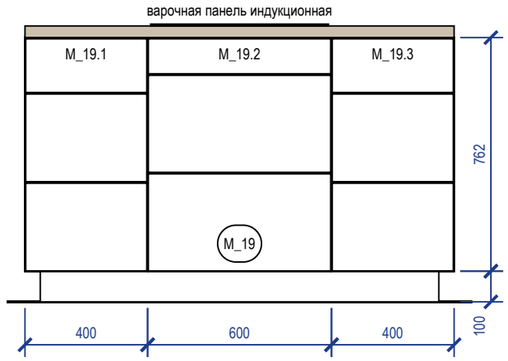

Вид без фасадов (наполнение, вывод)

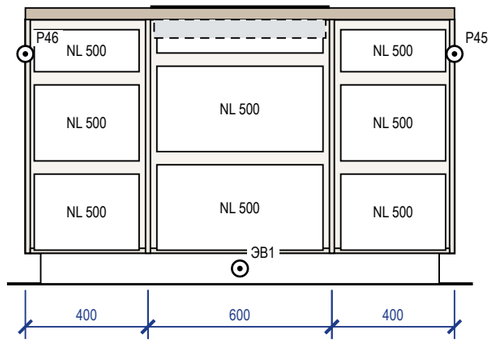

Разрез 1-1 через варочную

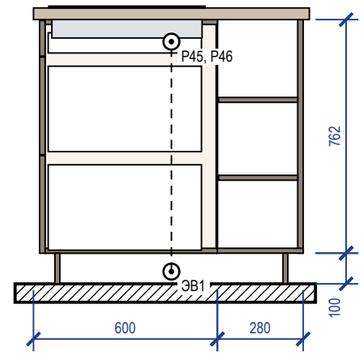

3D орто

Примечания

1. Размеры — в мм по чистовому полу; перед раскроем — контрольный замер цеха после укладки пола. Остров крепится к полу (уголки в цоколе), выравнивается опорами ±20 мм.
2. Корпуса — ЛДСП 16 мм, задняя стенка ХДФ 4 мм; фасады — МДФ, эмаль матовая 18 мм; столешница 38 мм (материал — по наименованию изделия: столешница травертин), свес 20 мм по периметру; цоколь 100 мм с отступом 50 мм.
3. Кромка: скрытые торцы 0,4 мм, видимые 2 мм. Номинальные зазоры: между фасадами 3 мм, фасад — столешница 3 мм.
4. Рабочая сторона — западная (к стене Г): проход 1240 мм; с тыла — открытые полки глубиной 262 мм. Членение и сторона — предложение мебельщика.
5. Варочная панель индукционная 60 см: вырез 560×490, передняя кромка выреза в 60 мм от рабочего края; верхний ящик под панелью — с зазором 40 мм под корпус панели (вентиляция индукции); размеры выреза — по шаблону выбранной модели.
6. Питание: ЭВ1 — варочная панель на острове — вывод из пола под островом, в цоколе; P45 — столешница острова — в торцевой панели, H=750; P46 столешница острова — в торцевой панели, H=750; кабель — внутри модуля до панели, доступ через съёмный цоколь.
7. Вытяжка над островом — островная потолочная, режим рециркуляции (угольный фильтр), ширина 900, низ +1550; низ — не ниже 650 мм над панелью или по паспорту модели.

Спецификация изделия M_19

Поз.	Наименование	Тип, размер	Кол.
M_19.1	модуль с ящиками	400×900×900	1
M_19.2	модуль под варочную панель	600×900×900	1
M_19.3	модуль с ящиками	400×900×900	1
M_19.2	Варочная панель индукционная, 60 см	вырез 560 × 490, кромка выреза в 60 от рабочего края	1
	Направляющие полного выдвижения с доводчиком NL 500	пара	9
	Ручка-профиль	латунь матовая	9
	Опора кухонная регулируемая 100–120 мм	+ клипса цоколя	12
	Уголок крепления острова к полу	стальной, в цоколе	4
	Полкодержатель с фиксацией	ø5 мм	24

					Проект: Квартира с кабинетом	**M 1:20**
	Лист	№ док.	Подпись	Дата		
Дизайнер	Кырлан А.С.			04.11.26	Остров M_19 (пом. 4). Чертёж изделия	Стадия: П; Лист: Д_10; Листов: 127

Ведомость отделки помещений (форма 1 прил. А ГОСТ 21.501-2018). Лист 1 из 2

№	Наименование помещения	Потолок			Стены и перегородки			Низ стен (плинтус)			Пол		Примечание
		Вид отделки	Код цвета	S, м²	Вид отделки	Код цвета	S, м²	Вид отделки	Код цвета	L, м	Вид отделки	S, м²	
1	Спальня 17,89 м²	ГКЛ по каркасу П113, отм. +2,500; +2,600; окраска, Tikkurila Anti-Reflex 2, глубокоматовая, 2 слоя, подготовка Q3	Tikkurila V503	17,89	Окраска, Farrow & Ball Modern Emulsion, матовая, 2 слоя, подготовка Q3 Акцент — стена А: окраска, Farrow & Ball Modern Emulsion, матовая, 2 слоя, подготовка Q3	Farrow & Ball No. 15 Farrow & Ball No. 34	29,37 6,55	Плинтус МДФ h=80 мм, аналог: МДФ под покраску 80×16	Farrow & Ball No. 15	16,2	Инженерная доска, 1167-4250, 2100×127 мм, на клею; тип 1, отм. ЧП ±0,000	17,89	Н стен 2500 (до потолка); плинтус в цвет: стены
2	Гардеробная-постирочная 5,11 м²	Существующий потолок, отм. +2,700; окраска, Tikkurila Anti-Reflex 2, глубокоматовая, 2 слоя, подготовка Q3	Tikkurila V503	5,11	Окраска, Tikkurila Harmony, матовая, 2 слоя, подготовка Q3	Tikkurila V503	22,94	Плинтус МДФ h=80 мм, аналог: МДФ под покраску 80×16	Tikkurila V503	8,3	Инженерная доска, 1167-4250, 2100×127 мм, на клею; тип 1, отм. ЧП ±0,000	5,11	Н стен 2700 (до потолка); плинтус в цвет: стены
3	Кабинет 18,92 м²	ГКЛ по каркасу П113, отм. +2,500; +2,600; окраска, Tikkurila Anti-Reflex 2, глубокоматовая, 2 слоя, подготовка Q3	Tikkurila V503	18,92	Окраска, Farrow & Ball Modern Emulsion, матовая, 2 слоя, подготовка Q3 Акцент — стена А: окраска, Farrow & Ball Modern Emulsion, матовая, 2 слоя, подготовка Q3	Farrow & Ball No. 15 Farrow & Ball No. 34	33,01 5,04	Плинтус МДФ h=80 мм, аналог: МДФ под покраску 80×16	Farrow & Ball No. 15	16,7	Инженерная доска, 1167-4250, 2100×127 мм, на клею; тип 1, отм. ЧП ±0,000	18,92	Н стен 2500 (до потолка); плинтус в цвет: стены
4	Кухня-гостиная 45,51 м²	ГКЛ по каркасу П113, отм. +2,600; +2,500; окраска, Tikkurila Anti-Reflex 2, глубокоматовая, 2 слоя, подготовка Q3	Tikkurila V503	45,51	Окраска, Farrow & Ball Modern Emulsion, матовая, 2 слоя, подготовка Q3 Акцент — стена А: окраска, Farrow & Ball Modern Emulsion, матовая, 2 слоя, подготовка Q3 Фартук кухни (стена А): облицовка керамогранитом, аналог: керамогранит под травертин, матовый, 1200×600×9 мм, клей C2 TE S1, затирка CG2WA	Farrow & Ball No. 15 Farrow & Ball No. 34 по артикулу	46,70 14,92 0,70	Плинтус МДФ h=80 мм, аналог: МДФ под покраску 80×16	Farrow & Ball No. 15	25,9	Инженерная доска, 1167-4250, 2100×127 мм, на клею; тип 1, отм. ЧП ±0,000	45,51	Н стен 2600 (до потолка); матовая моющаяся, класс 1 EN 13300 — осознанно вместо полуматовой; плинтус в цвет: стены
5	Коридор 9,07 м²	ГКЛ по каркасу П113, отм. +2,600; окраска, Tikkurila Anti-Reflex 2, глубокоматовая, 2 слоя, подготовка Q3	Tikkurila V503	9,07	Окраска, Farrow & Ball Modern Emulsion, матовая, 2 слоя, подготовка Q3	Farrow & Ball No. 15	31,82	Плинтус МДФ h=80 мм, аналог: МДФ под покраску 80×16	Farrow & Ball No. 15	11,2	Инженерная доска, 1167-4250, 2100×127 мм, на клею; тип 1, отм. ЧП ±0,000	9,07	Н стен 2600 (до потолка); матовая моющаяся, класс 1 EN 13300 — осознанно вместо полуматовой; плинтус в цвет: стены
6	Детская 9,97 м²	ГКЛ по каркасу П113, отм. +2,500; +2,600; окраска, Tikkurila Anti-Reflex 2, глубокоматовая, 2 слоя, подготовка Q3	Tikkurila V503	9,97	Окраска, Farrow & Ball Modern Emulsion, матовая, 2 слоя, подготовка Q3 Акцент — стена А: окраска, Farrow & Ball Modern Emulsion, матовая, 2 слоя, подготовка Q3	Farrow & Ball No. 15 Farrow & Ball No. 34	18,48 7,42	Плинтус МДФ h=69 мм, SX165	Farrow & Ball No. 15	12,0	Инженерная доска, 1167-4250, 2100×127 мм, на клею; тип 1, отм. ЧП ±0,000	9,97	Н стен 2500 (до потолка); плинтус в цвет: стены
7	Ванная 8,44 м²	ГКЛВ по каркасу П113, отм. +2,600; окраска, Tikkurila Luja 7, матовая, 2 слоя, подготовка Q3	Tikkurila V503	8,44	Облицовка плиткой, A8UZ, 600×1200×9 мм, клей C2 TE S1, затирка CG2WA	Atlas Concorde A8UZ	28,76	нет			Аналог: керамогранит ректифицированный под травертин, матовый, 600×600×9 мм; тип 2, отм. ЧП −0,015	8,44	Н стен 2615 (до потолка); гидроизоляция обмазочная, 2 слоя, с заведением на стены 200 мм; над ванной — до 2000 и 300 мм за борт (по пирогу пола); тест проливом и акт скрытых работ
8	Прихожая 7,89 м²	ГКЛ по каркасу П113, отм. +2,600; окраска, Tikkurila Anti-Reflex 2, глубокоматовая, 2 слоя, подготовка Q3	Tikkurila V503	7,89	Окраска, Farrow & Ball Modern Emulsion, матовая, 2 слоя, подготовка Q3	Farrow & Ball No. 15	20,40	Плинтус МДФ h=80 мм, аналог: МДФ под покраску 80×16	Farrow & Ball No. 15	7,0	Керамогранит, A8UZ, 600×1200×9 мм; тип 3, отм. ЧП ±0,000	7,89	Н стен 2600 (до потолка); матовая моющаяся, класс 1 EN 13300 — осознанно вместо полуматовой; плинтус в цвет: стены
9	Санузел гостевой 4,49 м²	ГКЛВ по каркасу П113, отм. +2,600; окраска, Tikkurila Luja 7, матовая, 2 слоя, подготовка Q3	Tikkurila V503	4,49	Облицовка плиткой, A8UZ, 600×1200×9 мм, клей C2 TE S1, затирка CG2WA	Atlas Concorde A8UZ	21,44	нет			Аналог: керамогранит ректифицированный под травертин, матовый, 600×600×9 мм; тип 2, отм. ЧП −0,015	4,49	Н стен 2615 (до потолка); гидроизоляция обмазочная, 2 слоя, по всему помещению, с заведением на стены 200 мм; у душа — на всю высоту стен душевой зоны и 500 мм за край душевой зоны (по пирогу пола); тест проливом и акт скрытых работ

Примечания

1. Ведомость продолжена на листе 2 из 2; итоги, сводка площадей и примечания — на последнем листе ведомости.

					Проект: Квартира с кабинетом
	Лист	№ док.	Подпись	Дата	
Дизайнер	Кырлан А.С.			04.11.26	Ведомость отделки помещений. Лист 1 из 2

Стадия	Лист	Листов
П	С1	127

Ведомость отделки помещений (форма 1 прил. А ГОСТ 21.501-2018). Лист 2 из 2

№	Наименование помещения	Потолок			Стены и перегородки			Низ стен (плинтус)			Пол		Примечание
		Вид отделки	Код цвета	S, м²	Вид отделки	Код цвета	S, м²	Вид отделки	Код цвета	L, м	Вид отделки	S, м²	
	Итого			**127,29**			**287,56**			**97,3**		**127,29**	

Сводка площадей по материалам отделки

Поверхность	Материал / код цвета	Серия	Площадь, м²
Потолок	Tikkurila V503	Anti-Reflex 2	114,36
Потолок	Tikkurila V503	Luja 7	12,93
Стены	Farrow & Ball No. 15	Modern Emulsion	179,79
Стены	Farrow & Ball No. 34	Modern Emulsion	33,93
Стены	Tikkurila V503	Harmony	22,94
Стены	облицовка плиткой 600×1200×9 мм, Atlas Concorde A8UZ	A8UZ	50,20
Фартук	облицовка керамогранитом 1200×600×9 мм	аналог: керамогранит под травертин, матовый	0,70

Примечания

1. Площади поверхностей — по чистым граням стен до отделки: стены = периметр × высоту от чистого пола помещения до низа потолка минус проёмы (облицовка плиткой — до верха облицовки); плинтус = периметр минус дверные проёмы; пол и потолок — по площади помещения. Количество плиток по раскладке. Площади помещений — с учётом всех частей помещения; откосы в площадь стен не входят.
2. Акцентные стены и фартук — отдельными строками, их площадь вычтена из основной отделки стен помещения; фартук — над нижними модулями кухни от столешницы до низа навесных шкафов, где шкафов нет — на 600 мм.
3. Плинтус — длина по периметру за вычетом дверных проёмов; примыкания к наличникам и встроенной мебели — по развёрткам.
4. Формат плитки — Ш×В×Т (ширина × высота в положении укладки × толщина), мм; на полу — вдоль стен А/В × вдоль стен Б/Г.
5. Коды цвета — по веерам производителей; колеровка каждой краски одной партией, проверка выкраса при свете D65 и при лампах проекта.
6. Уровни подготовки Q1–Q4 — система Knauf, не норма ГОСТ/СП; допуски поверхностей — по СП 71.13330.2017 (действующая редакция).
7. «аналог:» — изделие задано характеристиками, марку и артикул согласовать с заказчиком до закупки.

					Проект: Квартира с кабинетом		
	Лист	№ док.	Подпись	Дата	Ведомость отделки помещений. Лист 2 из 2	Стадия	Лист	Листов
Дизайнер	Кырлан А.С.			04.11.26		П	С2	127

Поз.	Наименование и техническая характеристика	Тип, марка, обозначение документа	Код продукции	Поставщик	Ед. изм.	Кол.	Образец	Примечание
	Лакокрасочные материалы							
1	Краска интерьерная водно-дисперсионная акриловая для стен, матовая, класс мокрого истирания 1 по EN 13300, база A; цвет по вееру Farrow & Ball No. 15 «Bone — мягкий каменно-серый с зеленцой», колеровка машинная	Farrow & Ball Modern Emulsion		Farrow & Ball	л	50		поз. К1 колерной карты; пом. 1, 3, 4, 5, 6, 8; S = 179,8 м² × 2 сл. × 0,12 л/м² = 43,1 л, +10 % и 0,5 л на подкраску → ≥ 48,0 л; тара 10 × 5 л
2	Краска интерьерная водно-дисперсионная акриловая для акцентных стен, матовая, класс мокрого истирания 1 по EN 13300, база C; цвет по вееру Farrow & Ball No. 34 «Calke Green — традиционный шалфей», колеровка машинная	Farrow & Ball Modern Emulsion		Farrow & Ball	л	10		поз. К2 колерной карты; пом. 1, 3, 4, 6; S = 33,9 м² × 2 сл. × 0,12 л/м² = 8,1 л, +10 % и 0,5 л на подкраску → ≥ 9,5 л; тара 2 × 5 л
3	Краска интерьерная водно-дисперсионная акриловая для потолков, глубокоматовая, класс мокрого истирания 2 по EN 13300, база A; цвет по вееру Tikkurila V503 «Winter», колеровка машинная	Tikkurila Anti-Reflex 2		Tikkurila	л	31,5		поз. К3 колерной карты; пом. 1, 2, 3, 4, 5, 6, 8; S = 114,4 м² × 2 сл. × 0,12 л/м² = 27,4 л, +10 % и 0,5 л на подкраску → ≥ 30,7 л; тара 3 × 9 л + 1 × 2,7 л + 2 × 0,9 л
4	Краска интерьерная водно-дисперсионная акриловая для стен, матовая, класс мокрого истирания 1 по EN 13300, база A; цвет по вееру Tikkurila V503 «Winter», колеровка машинная	Tikkurila Harmony		Tikkurila	л	7,2		поз. К5 колерной карты; пом. 2; S = 22,9 м² × 2 сл. × 0,12 л/м² = 5,5 л, +10 % и 0,5 л на подкраску → ≥ 6,6 л; тара 2 × 2,7 л + 2 × 0,9 л
5	Краска интерьерная водно-дисперсионная акриловая для потолков, матовая, класс мокрого истирания 1 по EN 13300, база A; цвет по вееру Tikkurila V503 «Winter», колеровка машинная	Tikkurila Luja 7		Tikkurila	л	4,5		поз. К8 колерной карты; пом. 7, 9; S = 12,9 м² × 2 сл. × 0,12 л/м² = 3,1 л, +10 % и 0,5 л на подкраску → ≥ 3,9 л; тара 1 × 2,7 л + 2 × 0,9 л
6	Краска для МДФ и дерева в цвет Farrow & Ball No. 15 «Bone — мягкий каменно-серый с зеленцой» — окраска плинтуса; блеск не ниже блеска стен	марка не задана			л	2,3		поз. К4, К7; пом. 1, 3, 4, 5, 6, 8; L = 89,0 м, S = 8,4 м² × 2 сл. × 0,12 л/м² + 10 %; продукт подобрать в веере Farrow & Ball
7	Краска для МДФ и дерева в цвет Tikkurila V503 «Winter» — окраска плинтуса; блеск не ниже блеска стен	марка не задана			л	0,5		поз. К6; пом. 2; L = 8,3 м, S = 0,8 м² × 2 сл. × 0,12 л/м² + 10 %; продукт подобрать в веере Tikkurila
8	Грунтовка акриловая под окраску стен и потолков — из системы производителя краски	по системе краски			м²	364		площадь окраски стен, акцентов и потолков; 1 слой перед окраской; расход — по ТУ грунтовки
	Плитка и керамогранит							
9	Керамогранит под травертин, 600×600×9 мм, ректификат, водопоглощение 0,1 % (BIa), противоскольжение R10, PEI IV	аналог по характеристикам			м²	18,36		шов 2 мм; Ванная, пол; Санузел гостевой, пол; по раскладке 46 шт (S = 12,93 м²), с запасом 51 шт
10	A8UZ, 600×1200×9 мм, ректификат, водопоглощение 0,1 % (BIa), противоскольжение R10, PEI IV	A8UZ		Atlas Concorde	м²	111,60		шов 2 мм; Ванная, стены А–Г; Ванная, короб инсталляции; Санузел гостевой, стены А–Г; Санузел гостевой, короб инсталляции; Прихожая, пол; по раскладке 137 шт (S = 59,81 м²), с запасом 155 шт
11	Керамогранит под травертин, матовый, 1200×600×9 мм, ректификат, водопоглощение 0,1 % (BIa)	аналог по характеристикам			м²	2,16		шов 2 мм; Кухня-гостиная, фартук (ст. А); по раскладке 2 шт (S = 0,70 м²), с запасом 3 шт
	Напольные покрытия							
12	1167-4250, рабочий слой 4 мм, эмиссия E1, укладка на клей	1167-4250		Coswick	м²	114		пом. 1, 2, 3, 4, 5, 6; S = 106,47 м² + 7 % (прямая укладка); к заказу — кратно упаковке
13	Клей для паркета и инженерной доски, эластичный (СМП / полиуретановый)	по рекомендации производителя доски			м²	107		площадь приклейки; расход и шпатель — по ТУ клея
	Погонажные изделия							
14	Плинтус МДФ под покраску 80×16, крепление к стене, окраска в цвет Farrow & Ball No. 15	аналог по характеристикам			м	85		пом. 1, 3, 4, 5, 8; L = 77,0 м (периметр без дверных проёмов) + 10 % на подрезку; в штуках — по длине планки
15	Плинтус МДФ под покраску 80×16, крепление к стене, окраска в цвет Tikkurila V503	аналог по характеристикам			м	10		пом. 2; L = 8,3 м (периметр без дверных проёмов) + 10 % на подрезку; в штуках — по длине планки
16	SX165, h = 69 мм, крепление к стене, окраска в цвет Farrow & Ball No. 15	SX165		Orac Decor	м	14		пом. 6; L = 12,0 м (периметр без дверных проёмов) + 10 % на подрезку; в штуках — по длине планки
	Смеси и материалы для облицовки							
17	Затирка для швов плитки, класс CG2WA по EN 13888	Mapei Ultracolor Plus 132		Mapei	кг	6		по раскладке (a+b)/(a·b) × шов × t × 1,6 + 10 %; в т. ч. 0,7 кг — позиции раскладки без марки
18	Клей плиточный C2 TE S1 по EN 12004, слой 5 мм	Ceresit CM 17		Ceresit	кг	590		24 меш. по 25 кг; 1,5 кг/м² на 1 мм слоя + 10 %; в т. ч. 70 кг — позиции раскладки без марки
19	Гидроизоляция обмазочная мокрых зон: пол, стены по периметру, зоны замачивания; 2 слоя с армирующей лентой в углах	аналог по характеристикам			м²	33		площадь по листу раскладки плитки + 10 %; расход смеси — по ТУ
20	Лента демпферная по периметру пола из плитки	аналог по характеристикам			м	28		периметр без дверных проёмов + 10 %

Примечания

1. Количества — из геометрии проекта: площади поверхностей по чистым граням стен до отделки (те же, что в ведомости отделки и колерной карте), плитка, клей и затирка — по раскладке плиточника; в графе «Кол.» — к заказу, с запасом.
2. Краска: расход 0,12 л/м² на слой в 2 слоя, если по ТУ не задан иной; запас 10 % и 0,5 л на подкраску каждого кода. Один код — одна партия, колеровка машинная в колеровочном центре бренда; в заказ — только после утверждения выкраса (колерная карта). Фасовка — по каталогу бренда на дату выпуска; к заказу — не меньше расчётного объёма.
3. «Аналог по характеристикам» — допускается изделие другого производителя с характеристиками не ниже указанных, по согласованию с автором проекта.
4. Графы «Код продукции» и «Масса 1 ед.» не заполнены: коды по классификатору продукции не присвоены, масса единицы до 25 кг (ГОСТ 21.110-2013).
5. Грунтовка и клей для доски указаны площадью обработки; объём — по ТУ выбранного продукта.

					Проект: Квартира с кабинетом
	Лист	№ док.	Подпись	Дата	
Дизайнер	Кырлан А.С.			04.11.26	Спецификация отделочных материалов

Стадия	Лист	Листов
П	С3	127

Список покупок: материалы для магазина

№	Что купить	Артикул или характеристика	Нужно с запасом	Брать в магазине	Фасовка	Уточнить в магазине	Помещения	Кто покупает
Покрытия полов и облицовка								
1	Инженерная доска (дуб натуральный, рабочий слой 4 мм, эмиссия E1, прямая укладка)	1167-4250	114,54 м²	114,6 м²		уточнить в магазине: м² в упаковке	1, 2, 3, 4, 5, 6	по проекту
2	Клей для паркетной и инженерной доски (эластичный, по ТУ изготовителя доски)	на выбор бригады по проекту	107,05 м²			уточнить в магазине: расход и фасовку — по выбранному продукту		бригада
3	Керамогранит 600×600 мм под травертин	по характеристике: керамогранит под травертин	51 шт	51 шт		уточнить в магазине: штук в коробке	7, 9	по проекту
4	Керамогранит 600×1200 мм A8UZ	A8UZ	151 шт	155 шт		уточнить в магазине: штук в коробке	7, 8, 9	по проекту
5	Керамогранит 1200×600 мм под травертин, матовый	по характеристике: керамогранит под травертин, матовый	3 шт	3 шт		уточнить в магазине: штук в коробке	4	по проекту
Сухие смеси и гидроизоляция								
6	Клей плиточный цементный класса C2 TE S1 (ГОСТ Р 56387-2018)	Ceresit CM 17 или аналог	589,59 кг	24 меш.	мешок 25 кг			по проекту
7	Затирка цементная класса CG2WA, цвет — по колерной карте	Mapei Ultracolor Plus 132 или аналог	5,98 кг	3 упак.	упак. 2 кг			по проекту
8	Гидроизоляция обмазочная полимерная, 2 слоя, лента в углах, манжеты на выводах	на выбор бригады по проекту	33,02 м²			уточнить в магазине: расход и фасовку — по выбранному продукту	7, 9	бригада
9	Лента демпферная по периметру пола из плитки	на выбор бригады по проекту	27,98 м	28 м		уточнить в магазине: фасовку		бригада
10	Смесь цементно-песчаная для стяжки М200 (50 мм, 33 мм)	на выбор бригады по проекту	6,5 м³			уточнить в магазине: расход и фасовку — по выбранному продукту		бригада
11	Смесь штукатурная гипсовая для машинного и ручного нанесения по маякам, слой до 10 мм	на выбор бригады по проекту	316,32 м²			уточнить в магазине: расход и фасовку — по выбранному продукту	1, 2, 3, 4, 5, 6, 7, 8, 9	бригада
Короба из ГКЛВ								
12	Лист ГКЛВ 12,5 мм, 2500 × 1200 мм, обшивка коробов в 2 слоя	на выбор бригады по проекту	9,35 м²	4 лист.	лист 3,00 м²		7, 9	бригада
13	Профиль стальной оцинкованный 27 × 28 мм: каркас коробов (стойки и направляющие)	на выбор бригады по проекту	20,02 м	7 шт	хлыст 3 м			бригада
Слаботочные сети								
14	Кабель домофона — тип по системе поставщика	на выбор бригады по проекту	5,7 м	6 м		уточнить в магазине: длину бухты		бригада
15	Кабель коаксиальный RG-6 (75 Ом) к розеткам ТВ	на выбор бригады по проекту	57 м	57 м		уточнить в магазине: длину бухты		бригада
16	Кабель U/UTP кат. 6 (LAN, Wi-Fi и камеры по PoE)	на выбор бригады по проекту	110,6 м	111 м		уточнить в магазине: длину бухты		бригада
17	Гофротруба Ø20 для слаботочных линий, отдельно от силовых	на выбор бригады по проекту	156 м	156 м		уточнить в магазине: длину бухты		бригада
18	Розетка компьютерная RJ45, кат. 6, с рамкой и подрозетником	на выбор бригады по проекту	5 шт	5 шт	шт			бригада
19	Розетка телевизионная (коаксиальная) с рамкой и подрозетником	на выбор бригады по проекту	3 шт	3 шт	шт			бригада

					Проект: Квартира с кабинетом
	Лист	№ док.	Подпись	Дата	Список покупок
Дизайнер	Кырлан А.С.			04.11.26	

Стадия	Лист	Листов
П	С4	127

Список покупок: материалы для магазина (продолжение)

№	Что купить	Артикул или характеристика	Нужно с запасом	Брать в магазине	Фасовка	Уточнить в магазине	Помещения	Кто покупает
20	Трубка или монитор домофона (поставка домофонной организации)	на выбор бригады по проекту	1 шт	1 шт	шт			по проекту
21	Щит слаботочный ЩС: корпус, DIN-рейка, розетки 220 В	на выбор бригады по проекту	1 шт	1 шт	шт			бригада
22	Патч-панель, портов не менее 7	на выбор бригады по проекту	1 шт	1 шт	шт			бригада
Лакокрасочные материалы								
23	Краска интерьерная акриловая, матовая, класс истирания 1	Farrow & Ball Modern Emulsion No. 34 «Calke Green — традиционный шалфей»	8,95 л	4 банк.	банка 2,5 л		1, 3, 4, 6	по проекту
24	Краска интерьерная акриловая, матовая, класс истирания 1	Farrow & Ball Modern Emulsion No. 15 «Bone — мягкий каменно-серый с зеленцой»	47,47 л	19 банк.	банка 2,5 л		1, 3, 4, 5, 6, 8	по проекту
25	Краска интерьерная акриловая, глубокоматовая, класс истирания 2	Tikkurila Anti-Reflex 2 V503 «Winter»	30,2 л	12 банк.	банка 2,7 л		1, 2, 3, 4, 5, 6, 8	по проекту
26	Краска интерьерная акриловая, матовая, класс истирания 1	Tikkurila Harmony V503 «Winter»	6,06 л	3 банк.	банка 2,7 л		2	по проекту
27	Краска интерьерная акриловая, матовая, класс истирания 1	Tikkurila Luja 7 V503 «Winter»	3,41 л	2 банк.	банка 2,7 л		7, 9	по проекту
28	Шпаклёвка финишная полимерная под окраску (стены и потолки, Q3)	на выбор бригады по проекту	400,35 м²			уточнить в магазине: расход и фасовку — по выбранному продукту		бригада
29	Грунтовка акриловая глубокого проникновения, 2 слоя	на выбор бригады по проекту	456,34 м²			уточнить в магазине: расход и фасовку — по выбранному продукту		бригада
Погонажные изделия и потолки								
30	Плинтус напольный МДФ под покраску, h=80 мм, крепление к стене	по характеристике: плинтус МДФ под покраску 80×16	93,92 м.п.	40 шт	хлыст 2,4 м		1, 2, 3, 4, 5, 8	по проекту
31	Плинтус напольный МДФ под покраску, h=69 мм, крепление к стене	SX165	13,16 м.п.	6 шт	хлыст 2,4 м		6	по проекту
32	Потолок подвесной ГКЛ/ГКЛВ по каркасу Knauf П113: листы, профили, подвесы, лента, шпаклёвка швов	Knauf П113	122,18 м²			уточнить в магазине: расход и фасовку — по выбранному продукту		по проекту

Примечания


1. «Нужно с запасом» — расход по чертежам и раскладке плюс запас на подрезку и подкраску; «Брать в магазине» — то же количество в единицах, которыми продают (банки, мешки, упаковки, листы, штуки, литры).
2. «Уточнить в магазине» — фасовки этого товара в проекте нет: спросите у продавца, сколько в упаковке, и возьмите целое число упаковок не меньше «Нужно с запасом».
3. Плитку, доску и краску одного цвета берите одной партией (один калибр и тон на помещение) и сохраните чек и номер партии до конца ремонта.
4. «По характеристике» — артикул не выбран: подойдёт любой товар с этими свойствами, согласуйте его с дизайнером до покупки. «Бригада» материал выбирает и закупает бригада по своей технологии.
5. Помещения: 1 — Спальня; 2 — Гардеробная-постирочная; 3 — Кабинет; 4 — Кухня-гостиная; 5 — Коридор; 6 — Детская; 7 — Ванная; 8 — Прихожая; 9 Санузел гостевой; «—» — материал для нескольких помещений, расход по месту.

					Проект: Квартира с кабинетом
	Лист	№ док.	Подпись	Дата	
Дизайнер	Кырлан А.С.			04.11.26	Список покупок (окончание)

Стадия	Лист	Листов
П	С5	127


1 Порог 15 мм: мокрая зона — смежное помещение (М 1:10)

Применение: двери Д-6, Д-7

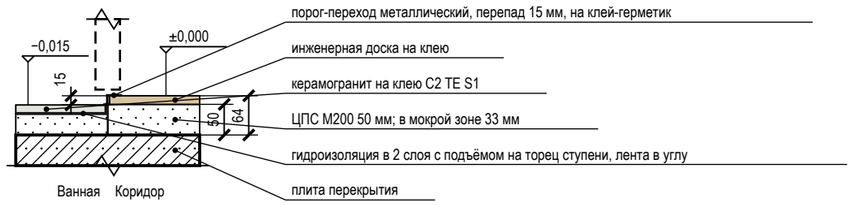


2 Дверь скрытого монтажа в плоскости стены, плинтус (М 1:5)

Применение: двери Д-2, Д-3, Д-4, Д-5, Д-6, Д-7

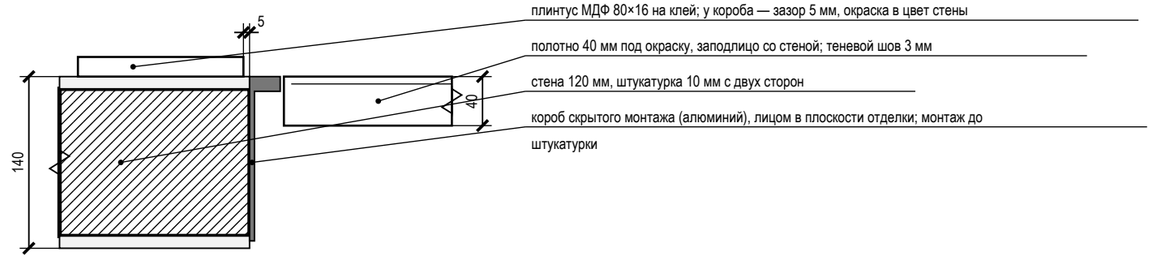


3 Короб стояков К1-1 с люком и звукоизоляцией (М 1:10)

Применение: пом. 9, 7, 4

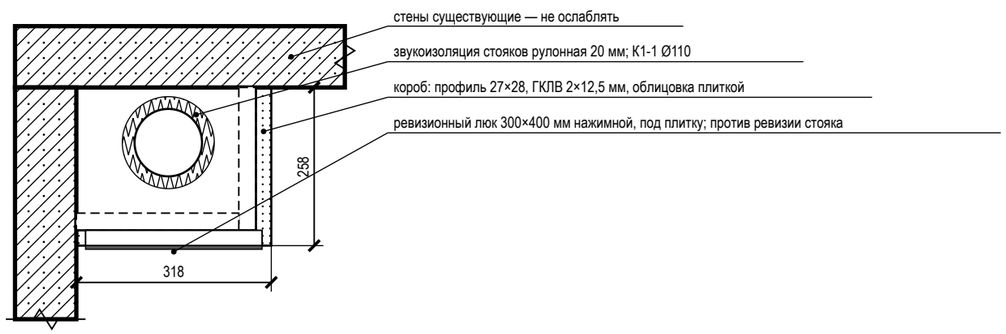


4 Гидроизоляция санузла: заход на стены 200 мм (М 1:20)

Применение: пом. 7, 9

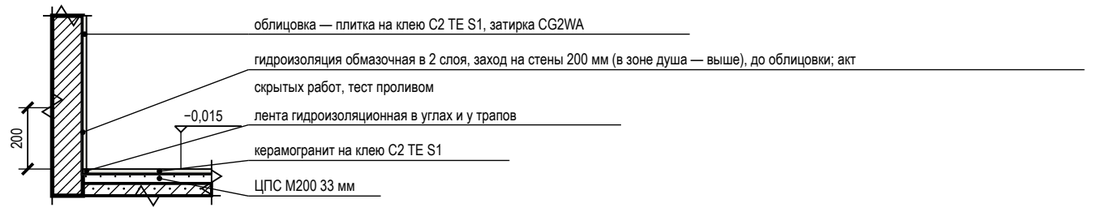


5 Плинтус МДФ 80×16 мм у окрашенной стены по доске (ламинату) (М 1:10)

Применение: пом. 1, 2, 3, 4, 5, 6

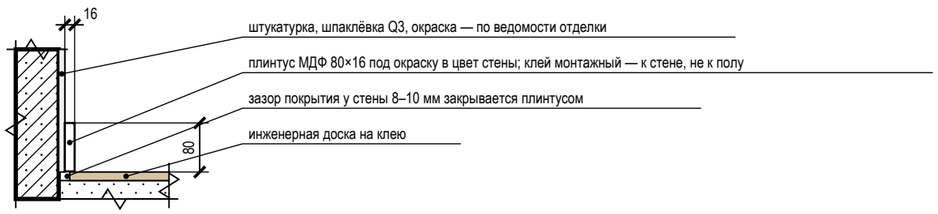

6 Плинтус МДФ 80×16 мм у окрашенной стены по керамограниту (плитке) (М 1:10)

Применение: пом. 8

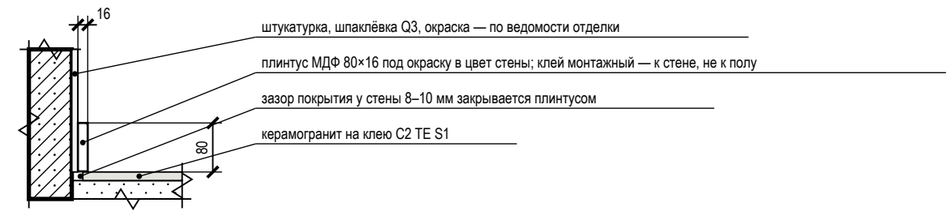

Условные обозначения

- железобетон (плита, стены) — условно: конструкция не установлена
- кладка, перегородка — условно: конструкция не установлена
- стяжка, раствор
- гипсокартон ГКЛВ
- звукоизоляция, эластичный заполнитель
- плитка, керамогранит на клею
- инженерная доска (покрытие пола)
- металлический профиль (порог, Т-профиль, короб двери)
- гидроизоляция (обмазочная, лента)

Примечания

1. Узлы — типовые решения проекта для мест, отмеченных выносками на листе схемы расположения развёрток и узлов; размеры — в мм, отметки — в м от ±0,000.
2. Узлы с гидроизоляцией, закладными и коробами скрытого монтажа принимаются по актам скрытых работ до закрытия отделкой; гидроизоляция — после теста проливом (24 ч).
3. Марки изделий (порог, Т-профиль, короб скрытой двери, люк) — по спецификациям; замена — на аналог с теми же габаритами по согласованию с автором проекта.
4. Материал плиты перекрытия и стен в узлах показан условно (железобетон, кладка): конструкция дома не установлена — крепёж, анкеры и толщины слоёв уточняются после обследования (до него — по допущениям общих указаний).

					Проект: Квартира с кабинетом
	Лист	№ док.	Подпись	Дата	Узлы
Дизайнер	Кырлан А.С.			04.11.26	

Стадия	Лист	Листов
П	С6	127