
LINEA

ДИЗАЙН-ПРОЕКТ ИНТЕРЬЕРА

# Четырёхкомнатная квартира

*13 помещений*

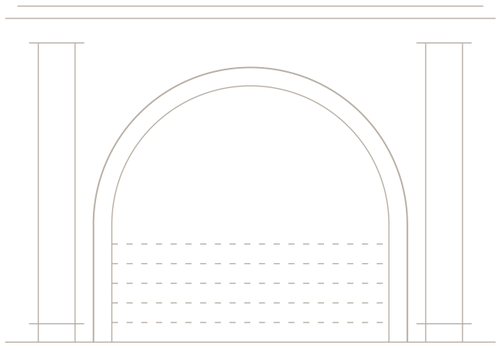


ПАЛИТРА ОТДЕЛКИ

| F497 | J484 | L481 | V486 | NCS S 3005-Y20 |
|---|---|---|---|---|
| 82 % | 12 % | 6 % | текстиль, декор | текстиль, декор |

АВТОР ПРОЕКТА

Кырлан Александр Сергеевич

Ноябрь 2026

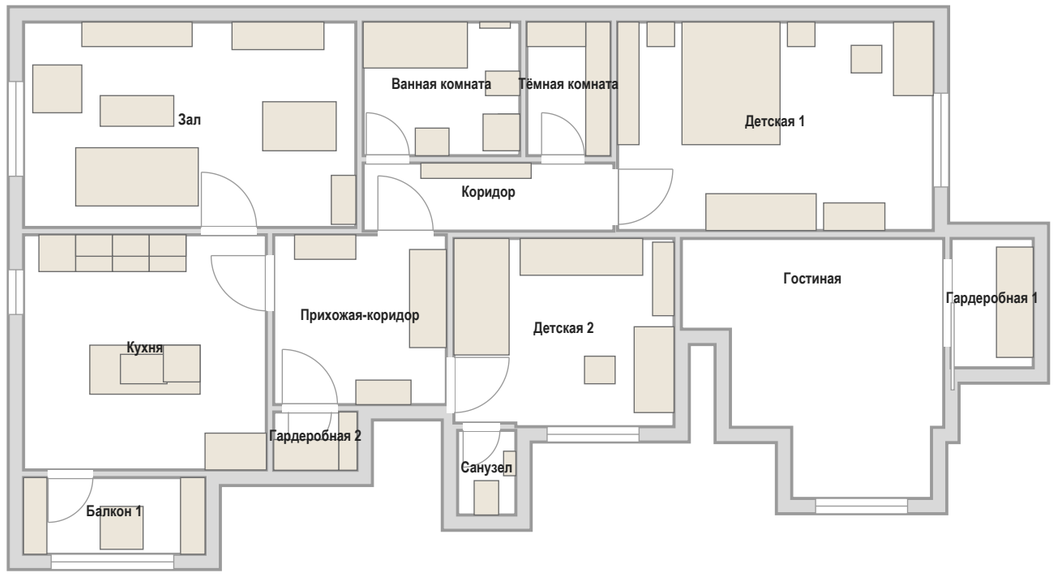


План расстановки мебели · М 1:100

| ОБЩАЯ ПЛОЩАДЬ | ПОМЕЩЕНИЙ | СТАДИЯ | ШИФР | ОСНОВА |
|---|---|---|---|---|
| 102,67 м² | 13, из них жилых 4 | Проект · предварительно | ГД-2026-004-АИ | план заказчика, без обмера |

Как оставить правку: кнопка «Правка к этому листу» в правом верхнем углу любого листа · все листы проекта: дизайн-студия-квартир.рф/review.html?p=gost-proekt2

выпуск 04.11.2026 № b23f08ad9b · стр. 1 из 120

## Объект

Четырёхкомнатная квартира: 106,37 м², помещений 13, из них жилых 4.

Стиль: современный (контемпорари) 100 %. Стадия: предварительный альбом без обмера, планировка по плану заказчика.

Открытых вопросов 27, конфликтов разделов 1; изменений утверждено 13, ждут подписи 7.

## Розетки и выводы

49 розеток (рамок 38), 5 выводов кабеля под технику и свет, 19 групп щита — всё с высотами от чистого пола: листы 41, 42, 43.

## Что решено (подписано вами)

ИЗ-1 — Окно на наружной стене В (1580…3080.

ИЗ-2 — Добавлены: бра Св63 у изголовья кровати М_33 (стена А, смещение 510, высота 1400 мм, 6 Вт, 2700 К, линия L21) и выключатель S17 (стена А, смещение 1050, высота 900 мм).

ИЗ-3 — Добавлен светильник Св64 над зеркалом ДК17 (стена Б, смещение 600, высота 1950 мм, 8 Вт, 3000 К, IP44, драйвер встроен, линия L12, группа 4).

ИЗ-4 — В S2 добавлен светорегулятор (тип ТЕ, под диммируемую ленту).

ИЗ-6 — Полотно раздвижное, две створки по 710 мм по накладной направляющей.

ИЗ-12 — Добавлены выводы к вентиляторам: ЭВ2 (ВР1, ванная комната) и ЭВ5 (ВР3, санузел) — группа 4, высота 2550 мм, IP44, включение с основным светом, таймер выбега в вентиляторе.

ИЗ-13 — Общей комнатой назначен «Зал» (18,16 м²): он больше «Гостиной», проходит норму общей комнаты не менее 16 м² (СП 54.13330.2022, п. 5.11) и по концепции интерьера несёт обеденную…

ИЗ-14 — Сохраняется существующее положение: вход в санузел — из «Детской 2», перепланировка с тамбуром не выполняется.

ИЗ-15 — Доля акцента 18 % принята: ТВ-стена А красится в L481 целиком, это замысел автора, на предметы акцент не переносится.

и ещё 4 — на листе реестра

## Что ждёт вашего ответа

К-1 — Окно детской 2 (поз. 9) на наружной стене В: привязки 1580…3080 в источниках нет — в экспликации скана окна этой комнаты не показано.

К-3 — Несущие стены не определены (нет плана БТИ и техзаключения): до их получения демонтаж не планируется.

К-4 — Гостиная (поз. 11): мебели в модели нет, расстановка ждёт решения заказчика.

К-5 — Гардеробная 1 (поз. 12) в натуре трапеция 2320/2132/1400, в модели прямоугольник той же площади: нужен контрольный обмер углов.

К-6 — Розетка Р7 (стиральная машина, ванная комната) стоит в 72 мм от угла при норме от 150 мм.

К-7 — Акцент L481 занимает больше порога 15 % площади поверхностей на акцентной стене А Гостиной — 16 % (проверка по доле акцента, замечание открыто намеренно).

К-8 — Графы «Пров.» и «Н. контр.» в штампе пусты: их заполняет человек, подписи проверяющего и нормоконтролёра автор проекта не ставит.

К-10 — Прямые углы помещений с кухней, санузлами, гардеробными и встроенной мебелью по скану не подтверждены (скос стен приведён к ступеням): ванная комната, тёмная комната, детская…

К-12 — Состав подрядчиков и поставщиков (кто покупает и кто монтирует радиаторы, подоконники, двери, розетки) от заказчика не получен.

К-13 — Детская 2: рабочий стол М_35 у стены Б получает боковой свет от окна справа от сидящего.

К-14 — Из чего стены под навесными шкафами — Ванная комната (стена Б, М_07), Кухня (стена А, М_23, М_24, М_25), Гардеробная 2 (стена В, М_32)? Проекта дома нет, на скане материал и…

К-15 — Стояки Ст К1-2 и Ст В1-2 (в данных (9400.

К-17 — Ведущий цвет — Paper F497 на стенах и потолке — занимает больше 80 % площади поверхностей в Тёмной комнате (87 %), Гардеробной 2 (89 %), Гардеробной 1 (86 %) и Балконе 1 (85…

К-18 — Вытяжка М_24 встроена в навесной модуль на отметке 1550 мм: её низ над электрической варочной панелью 610 мм, а фартук 650 мм при практике 450–600 мм.

и ещё 14 — на листе реестра

## Предложено, ждёт подписи

ИЗ-5 — Новая группа 19 «розетки гостиной»: автомат С16, УЗО 30 мА типа А, кабель ВВГнг(А)-LS 3×2,5, 1,0 кВт, длина линии 30 м (оценка, не замер).

ИЗ-7 — Конвейер заменял акцентную стену предметами и ради порога снял её.

ИЗ-8 — Ступени контура 14840, 7770, 6600, 8030 мм (+60 мм): приведены к крайним граням помещений модели (Детская 1, Санузел).

ИЗ-9 — Добавлены: слаботочный щит ЩС (Прихожая-коридор, стена А, смещение 1380, высота 1600 мм), точки доступа АР1 (5500.

ИЗ-10 — Назначение «вытяжка М_24 (в модуле, съёмная панель)» и признак доступа access: true (не считает розетку закрытой мебелью).

| | | | | | | | | |
|---|---|---|---|---|---|---|---|---|
| | | | | | Проект: Четырёхкомнатная квартира | | | |
| | Лист | № док. | Подпись | Дата | Ваш проект на одной странице | Стадия | Лист | Листов |
| Дизайнер | Кырлан А.С. | | | 04.11.26 | | П | 2 | 120 |

## Список листов


| Лист | Наименование |
|---|---|
| 1 | Титульный лист |
| 2 | Ваш проект на одной странице |
| 3 | Список листов |
| 4 | Список листов |
| 5 | Как читать альбом |
| 6 | План планировки от заказчика |
| 7 | План монтажный |
| 8 | Кухня (пом. 6). Монтажная схема |
| 9 | Кухня (пом. 6). Монтажная схема |
| 10 | Шкафы. Монтажная схема. Лист 1 из 3 |
| 11 | Шкафы. Монтажная схема. Лист 2 из 3 |
| 12 | Шкафы. Монтажная схема. Лист 3 из 3 |
| 13 | Карта покрытий стен |
| 14 | Колерная карта |
| 15 | Колерная карта |
| 16 | План размещения мебели и оборудования |
| 17 | Спецификация мебели и оборудования |
| 18 | Спецификация мебели и оборудования (продолжение) |
| 19 | Спецификация мебели и оборудования (продолжение) |
| 20 | Спецификация мебели и оборудования (продолжение) |
| 21 | Ведомости изделий, техники и фурнитуры |
| 22 | План выводов сантехники |
| 23 | Схема разводки водопровода и канализации |
| 24 | Аксонометрическая схема В1 (холодное водоснабжение) |
| 25 | Аксонометрическая схема Т3 (горячее водоснабжение) |
| 26 | Аксонометрическая схема К1 (канализация) |
| 27 | Развёртки мокрых зон: выводы ВК. Ванная комната (лист 1 из 2) |
| 28 | Развёртки мокрых зон: выводы ВК. Ванная комната (лист 2 из 2) |
| 29 | Развёртки мокрых зон: выводы ВК. Кухня |
| 30 | Развёртки мокрых зон: выводы ВК. Санузел |
| 31 | Спецификация сантехнического оборудования |
| 32 | Раскладка плитки. Ванная комната. Развёртки стен |
| 33 | Раскладка плитки. Санузел. Развёртки стен |
| 34 | План размещения дверей |
| 35 | Ведомость заполнения проёмов |
| 36 | План потолков |
| 37 | Разрезы и узлы потолков |
| 38 | Разрезы и узлы потолков (продолжение) |
| 39 | Сечения потолков М 1:10 |
| 40 | Сечения потолков М 1:10 |
| 41 | Однолинейная схема щита |
| 42 | Однолинейная схема щита (продолжение) |
| 43 | План розеток и электровыводов |
| 44 | План слаботочных сетей |
| 45 | План освещения |
| 46 | Техническое задание на подбор светильников |
| 47 | Управление светильниками |
| 48 | План вентиляции |
| 49 | План отопления |
| 50 | План покрытий пола |
| 51 | Раскладка плитки. Планы полов |
| 52 | Раскладка плитки. Фартук кухни |
| 53 | Развёртка стены А. Зал (пом. 1) |
| 54 | Привязки электроточек, стена А. Зал (пом. 1) |
| 55 | Развёртка стены Б. Зал (пом. 1) |
| 56 | Развёртка стены В. Зал (пом. 1) |
| 57 | Развёртка стены Г. Зал (пом. 1) |
| 58 | Развёртки стен А, Б. Ванная комната (пом. 2) |
| 59 | Развёртки стен В, Г. Ванная комната (пом. 2) |
| 60 | Привязки электроточек и выводов ВК, стены Б, В. Ванная комната (пом. 2) |


| | | | | | |
|---|---|---|---|---|---|
| | | | | | Проект: Четырёхкомнатная квартира |
| | Лист | № док. | Подпись | Дата | |
| Дизайнер | Кырлан А.С. | | | 04.11.26 | Список листов |
| | | | | | |

| Стадия | Лист | Листов |
|---|---|---|
| П | 3 | 120 |

выпуск 04.11.2026 № b23f08ad9b · стр. 3 из 120

## Список листов (продолжение)


| Лист | Наименование |
|---|---|
| 61 | Развёртки стен А, Б, В. Тёмная комната (пом. 3) |
| 62 | Развёртка стены Г. Тёмная комната (пом. 3) |
| 63 | Развёртка стены А. Детская 1 (пом. 4) |
| 64 | Развёртка стены Б. Детская 1 (пом. 4) |
| 65 | Развёртка стены В. Детская 1 (пом. 4) |
| 66 | Развёртка стены Г. Детская 1 (пом. 4) |
| 67 | Развёртки стен А, Б. Коридор (пом. 5) |
| 68 | Развёртка стены В. Коридор (пом. 5) |
| 69 | Развёртка стены А. Кухня (пом. 6), кухонный фронт |
| 70 | Привязки электроточек, стена А. Кухня (пом. 6) |
| 71 | Развёртка стены Б. Кухня (пом. 6) |
| 72 | Развёртка стены В. Кухня (пом. 6) |
| 73 | Развёртка стены Г. Кухня (пом. 6) |
| 74 | Развёртки стен А, Б. Прихожая-коридор (пом. 7) |
| 75 | Развёртки стен В, Г. Прихожая-коридор (пом. 7) |
| 76 | Развёртки стен А, Б, В. Гардеробная 2 (пом. 8) |
| 77 | Развёртка стены Г. Гардеробная 2 (пом. 8) |
| 78 | Развёртка стены А. Детская 2 (пом. 9) |
| 79 | Развёртка стены Б. Детская 2 (пом. 9) |
| 80 | Привязки электроточек, стена Б. Детская 2 (пом. 9) |
| 81 | Развёртка стены В. Детская 2 (пом. 9) |
| 82 | Развёртка стены Г. Детская 2 (пом. 9) |
| 83 | Развёртки стен А, Б, В. Санузел (пом. 10) |
| 84 | Привязки электроточек и выводов ВК, стена Б. Санузел (пом. 10) |
| 85 | Развёртка стены Г. Санузел (пом. 10) |
| 86 | Развёртка стены А. Гостиная (пом. 11) |
| 87 | Развёртка стены Б. Гостиная (пом. 11) |
| 88 | Развёртки стен В, Г. Гостиная (пом. 11) |
| 89 | Развёртки стен. Гардеробная 1 (пом. 12) |
| 90 | Развёртки стен А, Б. Балкон 1 (пом. 13) |
| 91 | Развёртки стен В, Г. Балкон 1 (пом. 13) |
| 92 | Открытые вопросы, принятые допущения и конфликты. Лист 1 из 5 |
| 93 | Открытые вопросы, принятые допущения и конфликты. Лист 2 из 5 |
| 94 | Открытые вопросы, принятые допущения и конфликты. Лист 3 из 5 |
| 95 | Открытые вопросы, принятые допущения и конфликты. Лист 4 из 5 |
| 96 | Открытые вопросы, принятые допущения и конфликты. Лист 5 из 5 |
| Д_1 | Система хранения М_07 |
| Д_2 | Система хранения М_08 |
| Д_3 | Система хранения М_09 |
| Д_4 | Шкаф распашной М_15 |
| Д_5 | Система хранения М_17 |
| Д_6 | Система хранения М_18 |
| Д_7 | Шкаф-купе М_28 |
| Д_8 | Система хранения М_31 |
| Д_9 | Система хранения М_32 |
| Д_10 | Шкаф распашной М_34 |
| Д_11 | Система хранения М_38 |
| Д_12 | Система хранения М_39 |
| Д_13 | Система хранения М_40 |
| Д_14 | Кухня (пом. 6). Развёртка гарнитура |
| Д_15 | Кухня (пом. 6). Развёртка гарнитура |
| Д_16 | Остров М_26 (пом. 6). Чертёж изделия |
| С1 | Ведомость отделки помещений. Лист 1 из 3 |
| С2 | Ведомость отделки помещений. Лист 2 из 3 |
| С3 | Ведомость отделки помещений. Лист 3 из 3 |
| С4 | Спецификация отделочных материалов |
| С5 | Спецификация отделочных материалов |
| С6 | Список покупок |
| С7 | Список покупок (окончание) |
| С8 | Узлы |


## Общие указания

1. Размеры даны в мм от чистовых поверхностей стен: слой штукатурки 20 мм по блоку и 5 мм шпаклёвки по ГКЛ учтён. Перед заказом встроенной мебели — контрольный обмер после штукатурки.
2. Привязки мебели — от стен и углов помещения, а не от другой мебели.
3. Розетки, выводы и выключатели под мебель — см. лист 43 «План розеток и электровыводов»; сантехприборы и выводы воды — лист 22.
4. План расстановки не является документацией для изготовления мебели: изделия — по чертежам мебельщика; покупную мебель заменять только на изделия не больше габарита из спецификации (лист 17).
5. Встроенная мебель «стена в стену» — с зазором 10 мм с каждой стороны или с компенсаторами.
6. Развёртки — вид на стену изнутри помещения, по часовой стрелке; расположение стен на схеме листа развёртки; размеры — в мм по чистовым поверхностям; отметки — в м от ±0,000; высоты Н — от чистого пола помещения до оси изделия, у декора — до центра.
7. Красная цепочка — привязки электроточек и выводов по осям от угла чистовых стен; высота Н — у знака, от чистого пола до оси; высоты мебели, проёмов и границ отделки колонкой отметок слева. Стена с 5 и более точками или с мелкими звеньями привязок показана двумя видами: архитектурная развёртка (мебель, отделка, проёмы, высоты) и вид «Привязки» на отдельном листе — точки и выводы с марками, одна цепочка по осям и таблица привязок (каждая точка — строка).
8. У знака электроточки: марка (Р — розетка, S — выключатель, Св — светильник, ЭВ вывод кабеля), ×N — число постов в рамке, гр. — группа щита, Н — высота оси от чистого пола, мм; группы по клавишам выключателя — на листе выключателей.
9. Схема мебели, приборов и декора не является технической документацией для производства мебели; габариты — по паспортам изделий.
10. Марки позиций: М_NN — мебель, ОБ_NN — оборудование, С_NN — сантехника; О-N отделка (ведомость отделочных материалов, серия С).
11. Размеры мебели и изделий на заказ уточнить по месту после отделочных работ.

| | | | | | |
|---|---|---|---|---|---|
| | | | | | Проект: Четырёхкомнатная квартира |
| | Лист | № док. | Подпись | Дата | |
| Дизайнер | Кырлан А.С. | | | 04.11.26 | Список листов |
| | | | | | Стадия: П; Лист: 4; Листов: 120 |

выпуск 04.11.2026 № b23f08ad9b · стр. 4 из 120

## Что в альбоме

Альбом — дизайн-проект с рабочими чертежами для ремонта. Листы идут в порядке работ: титул и вводные, реестр открытых вопросов и решений, планы (обмер, монтаж стен, мебель, двери, потолки, полы), инженерия (сантехника, электрика, вентиляция и отопление), развёртки стен с визуализациями помещений, чертежи мебели, ведомости материалов и узлы.

Вам как заказчику — титул, эта вводная, «Ваш проект на одной странице», реестр вопросов, план мебели, визуализации и развёртки, ведомости мебели и материалов. Подрядчику — всё остальное: монтажные планы, привязки выводов и розеток, узлы, ведомости объёмов.

## Знаки на листах

Без знака — решение утверждено или подтверждено обмером.

## Что проверить до ремонта

1. Розетки у кровати и рабочего места: хватает ли их с каждой стороны кровати и над столом (план розеток — лист 43).

2. Выводы под технику — варочная панель, духовка, посудомойка, стиральная машина, бойлер: совпадают ли с выбранными моделями (листы 17, 18, 19, 20, 43).

3. Высоты розеток, выключателей и выводов даны от чистого пола: если мебель или техника будут другими — скажите до штробления стен.

## Номера записей

К-N — открытый вопрос: чего не хватает или что выбрать (варианты и рекомендация — в тексте). Пока ответа нет, действует строка «если решения нет».

Кф-N — конфликт между разделами (например, мебель и радиатор в одном месте); закрывается решением, которое записывается как ИЗ-N.

ИЗ-N — изменение проекта: что было, что стало и кто утвердил. Изменение без подписи предложение.

Все записи — на листе реестра сразу после вводных; на других листах на них стоят ссылки.

## Почему альбом предварительный


Обмера на объекте не было: размеры взяты с плана заказчика. Технические условия (мощность, вода, вентиляция дома) не получены, часть решений ждёт вашего ответа. Пока в реестре есть открытые вопросы, альбом предварительный — пометка в штампе снимается закрытием вопросов, а не стиранием.

Правку к любому листу можно оставить по кнопке «Правка к листу» или на сайте студии: дизайн-студия-квартир.рф — укажите номер листа и что изменить.

3 круга правок входят в цену; условия — в договоре и на странице вашего заказа на сайте студии.

## Отметки по высоте

| | |
|---|---|
| **±0,000** | чистый пол пом. 1, 3–9, 11, 12; отсчёт высот |
| **−0,015** | чистый пол пом. 2, 10, ниже на 15 мм |
| **−0,030** | чистый пол пом. 13, ниже на 30 мм |
| **−0,170** | верх плиты — расчёт, не замер (задание на обмер) |
| **сущ. пол** | снимается до плиты; не замерен (задание на обмер) |

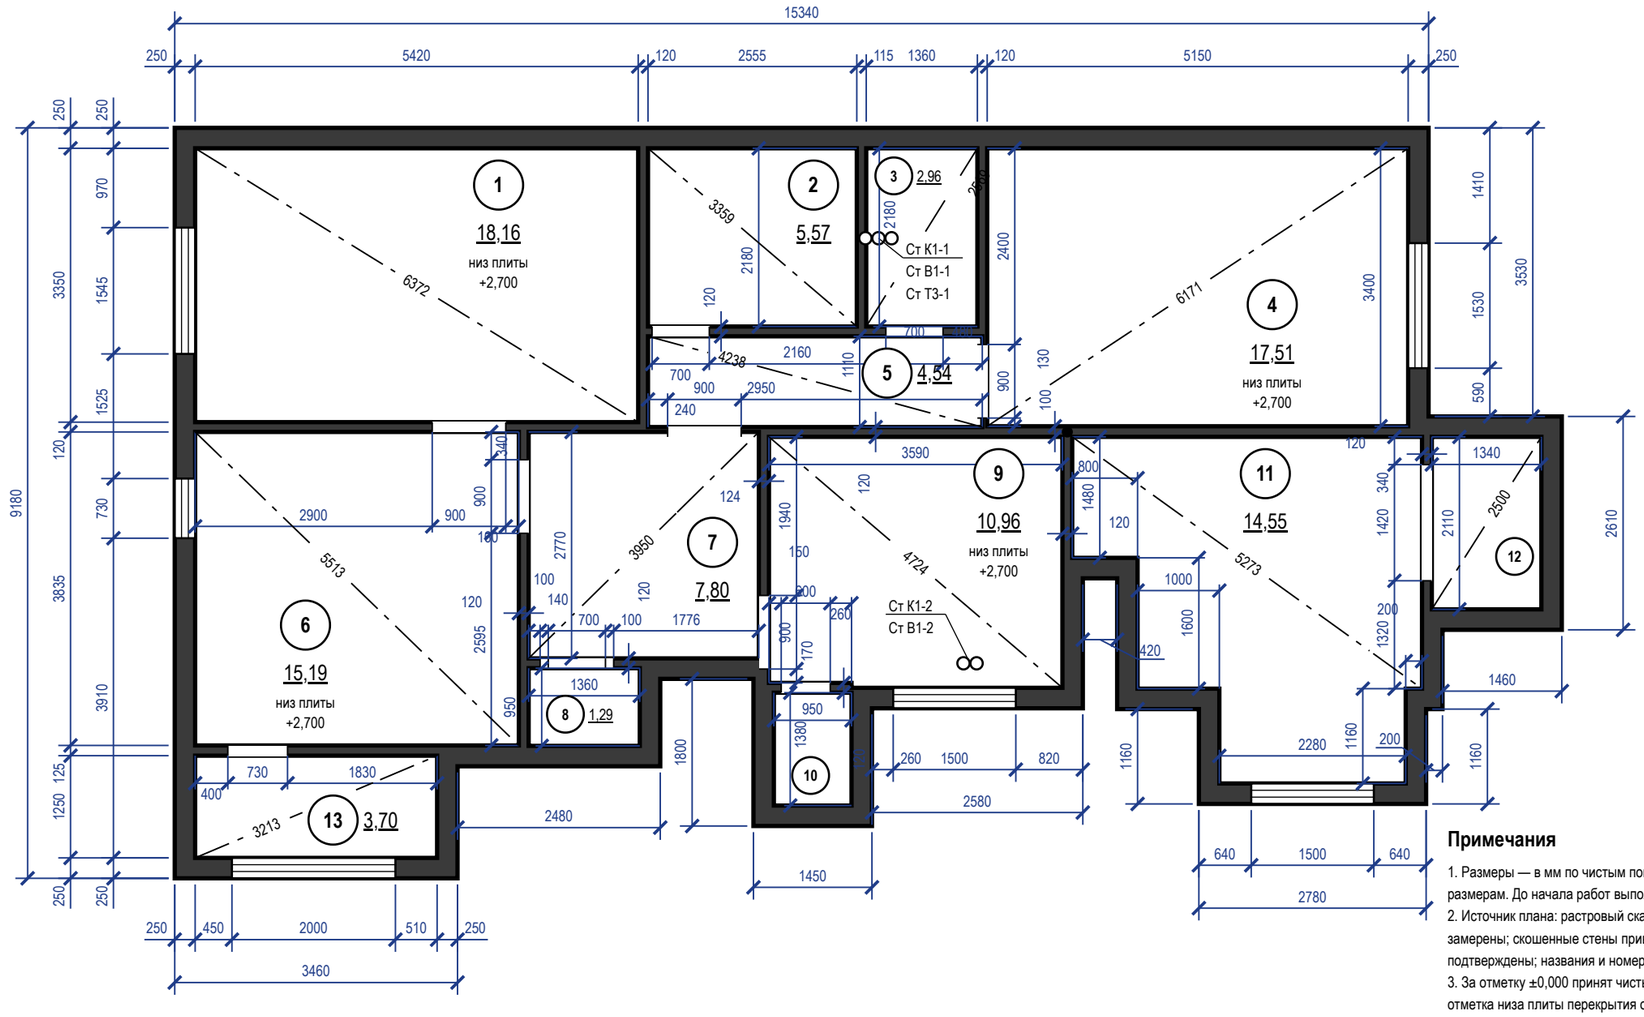


## Экспликация помещений

| № | Наименование | Площадь, м² |
|---|---|---|
| 1 | Зал | 18,16 |
| 2 | Ванная комната | 5,57 |
| 3 | Тёмная комната | 2,96 |
| 4 | Детская 1 | 17,51 |
| 5 | Коридор | 4,54 |
| 6 | Кухня | 15,19 |
| 7 | Прихожая-коридор | 7,80 |
| 8 | Гардеробная 2 | 1,29 |
| 9 | Детская 2 | 10,96 |
| 10 | Санузел | 1,31 |
| 11 | Гостиная | 14,55 |
| 12 | Гардеробная 1 | 2,83 |
| 13 | Балкон 1 * | 3,70 |
| | **Итого (общая площадь)** | **102,67** |


## Условные обозначения

- существующие стены (сечение)
- окно (рама, остекление)
- проём существующий, без заполнения (откосы)
- стояк: К1 — канализация, В1 — ХВС, Т3 — ГВС
- диагональ помещения — контроль прямоугольности
- (1) номер помещения, площадь м²

## Примечания

1. Размеры — в мм по чистым поверхностям стен до отделки (по плану заказчика); площади — в м² по тем же размерам. До начала работ выполнить контрольный обмер.
2. Источник плана: растровый скан плана заказчика, размеры сняты с размерных цепочек, на объекте не замерены; скошенные стены приведены к ступеням (на плане не натура), углы 90° и диагонали не подтверждены; названия и номера помещений со сканом не сверены.
3. За отметку ±0,000 принят чистый пол, не существующий (блок отметок). «Низ плиты» у марки помещения отметка низа плиты перекрытия от ±0,000, как на развёртках и плане потолков (не высота потолка: потолок по плану потолков).
4. Толщины стен: наружные 250 мм, перегородки 120 мм; отличающиеся толщины и уступы — размерами на плане.
5. Несущие стены не определены: до технического заключения все стены считать несущими; проёмы и штробы в них не выполнять.
6. Дверные проёмы показаны без заполнения (двери — лист 35); высота дверных проёмов 2100 мм; низ окон (подоконник) 800, 900 мм от чистого пола, высота окон 1600, 1700 мм.
7. Диагонали — контрольные размеры; расхождение более 5 мм подписать на плане как перекос.
8. Размеры проверить на месте до начала работ; расхождение контрольных промеров ≤ 2 %.
9. Помещения, отмеченные *, в общую площадь квартиры и в итоги не входят.
10. Размеры короче 1 мм на листе цепочкой не показаны (две выносные линии на таком расстоянии сливаются): пом. 5, стена А — 50 мм от угла до проёма.

| | | | | | |
|---|---|---|---|---|---|
| | | | | | Проект: Четырёхкомнатная квартира — **М 1:75** |
| | Лист | № док. | Подпись | Дата | План планировки от заказчика |
| Дизайнер | Кырлан А.С. | | | 04.11.26 | Стадия: П · Лист: 6 · Листов: 120 |

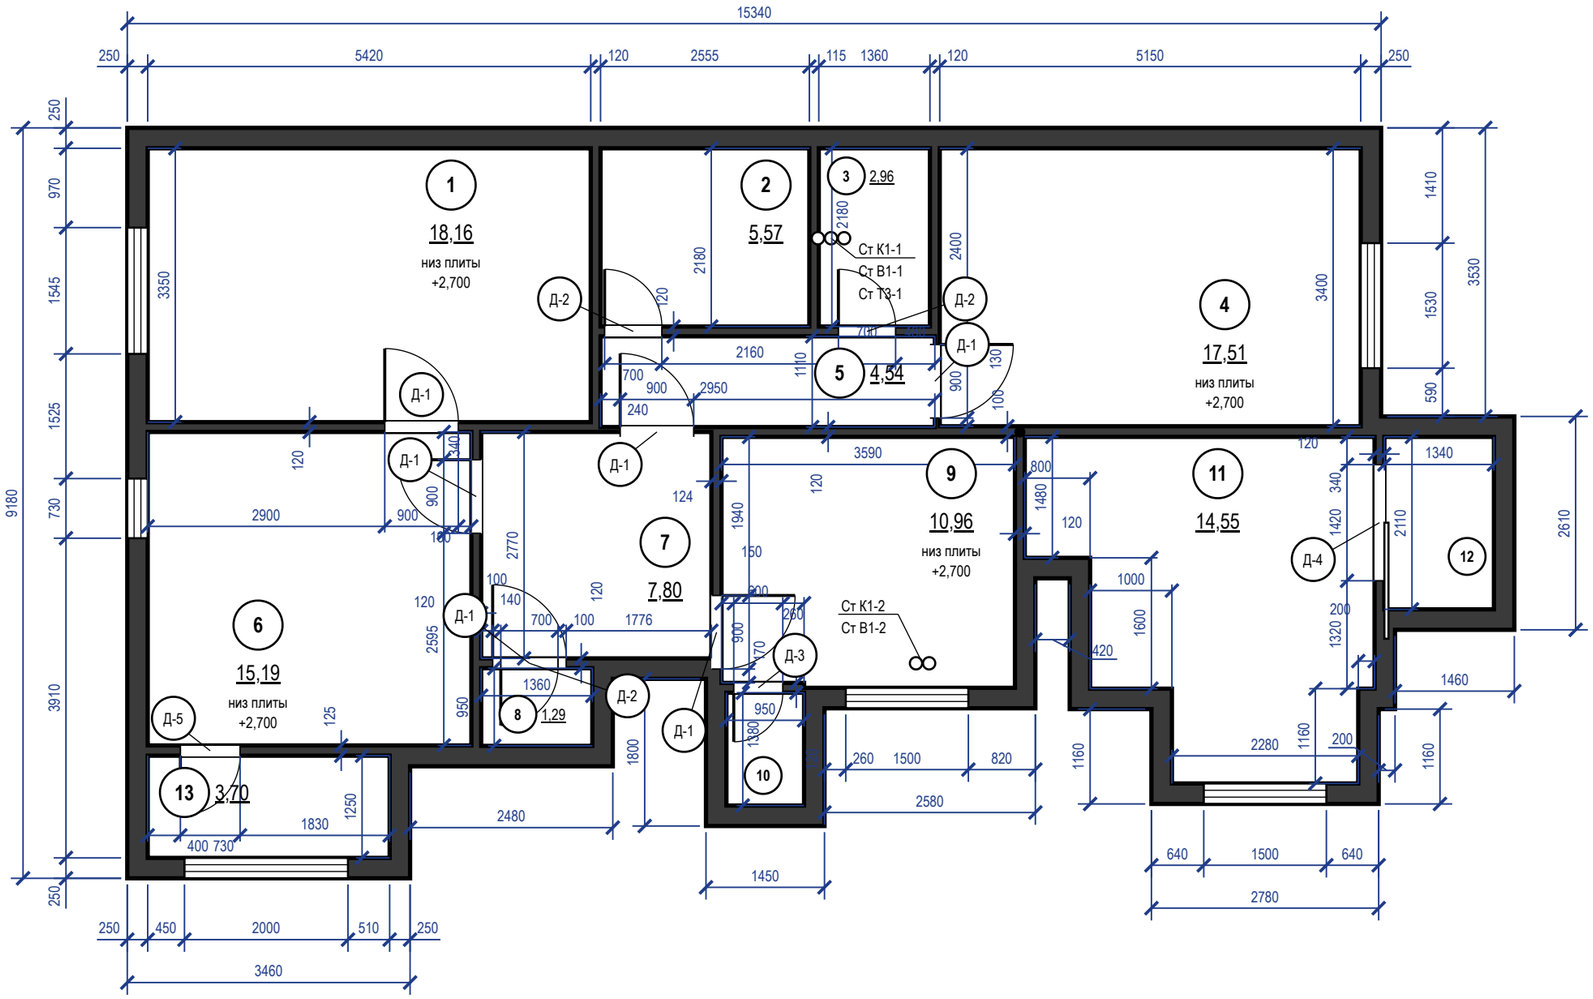


## Экспликация помещений

| № | Наименование | Площадь, м² |
|---|---|---|
| 1 | Зал | 18,16 |
| 2 | Ванная комната | 5,57 |
| 3 | Тёмная комната | 2,96 |
| 4 | Детская 1 | 17,51 |
| 5 | Коридор | 4,54 |
| 6 | Кухня | 15,19 |
| 7 | Прихожая-коридор | 7,80 |
| 8 | Гардеробная 2 | 1,29 |
| 9 | Детская 2 | 10,96 |
| 10 | Санузел | 1,31 |
| 11 | Гостиная | 14,55 |
| 12 | Гардеробная 1 | 2,83 |
| 13 | Балкон 1 * | 3,70 |
| | **Итого (общая площадь)** | **102,67** |

## Таблица проёмов

| Марка | Наименование | Проём ш×в, мм | Полотно (расч.) |
|---|---|---|---|
| Д-1 | Дверь распашная | 900×2100 | 800×2000 |
| Д-2 | Дверь распашная | 700×2100 | 600×2000 |
| Д-3 | Дверь распашная | 600×2100 | не задано (записи реестра нет) |
| Д-4 | Дверь раздвижная | 1420×2100 | не задано (записи реестра нет) |
| Д-5 | Дверь распашная | 730×2100 | не задано (записи реестра нет) |

## Примечания

1. Размеры — в мм от чистовых поверхностей стен до отделки; размеры уточнить по месту до начала работ.
2. Д-N, ПР-N в кружке — марка проёма: проём и полотно — по таблице проёмов, «расч.» полотно по проёму, заказ — по выбранной модели; ведомость, отделка и фурнитура — лист 35.
3. Несущие стены не изменять: проёмы, ниши и штробы в них — только по техническому заключению.
4. «расч.» — полотно, выведенное из проёма по запасу каталогов; заказ — по таблице проёмов выбранной модели; Д-1, Д-2: проём 2100, а под полотно 2000 по каталогам нужен 2040–2080, под 2100 — 2140–2180: высоту проёма — по модели; Д-3: проём 600×2100 вне ряда стандартных полотен — полотно задать при выборе модели; Д-4: раздвижная, полотно — по системе — полотно задать при выборе модели; Д-5: проём 730×2100 вне ряда стандартных полотен — полотно задать при выборе модели.
5. Размеры короче 1 мм на листе цепочкой не показаны (две выносные линии на таком расстоянии сливаются): пом. 5, стена А — 50 мм от угла до проёма.


| | | | | |
|---|---|---|---|---|
| | Лист | № док. | Подпись | Дата |
| Дизайнер | Кырлан А.С. | | | 04.11.26 |

Проект: Четырёхкомнатная квартира — **М 1:75**


План монтажный

| Стадия | Лист | Листов |
|---|---|---|
| П | 7 | 120 |

## Привязка выводов и крепление модулей

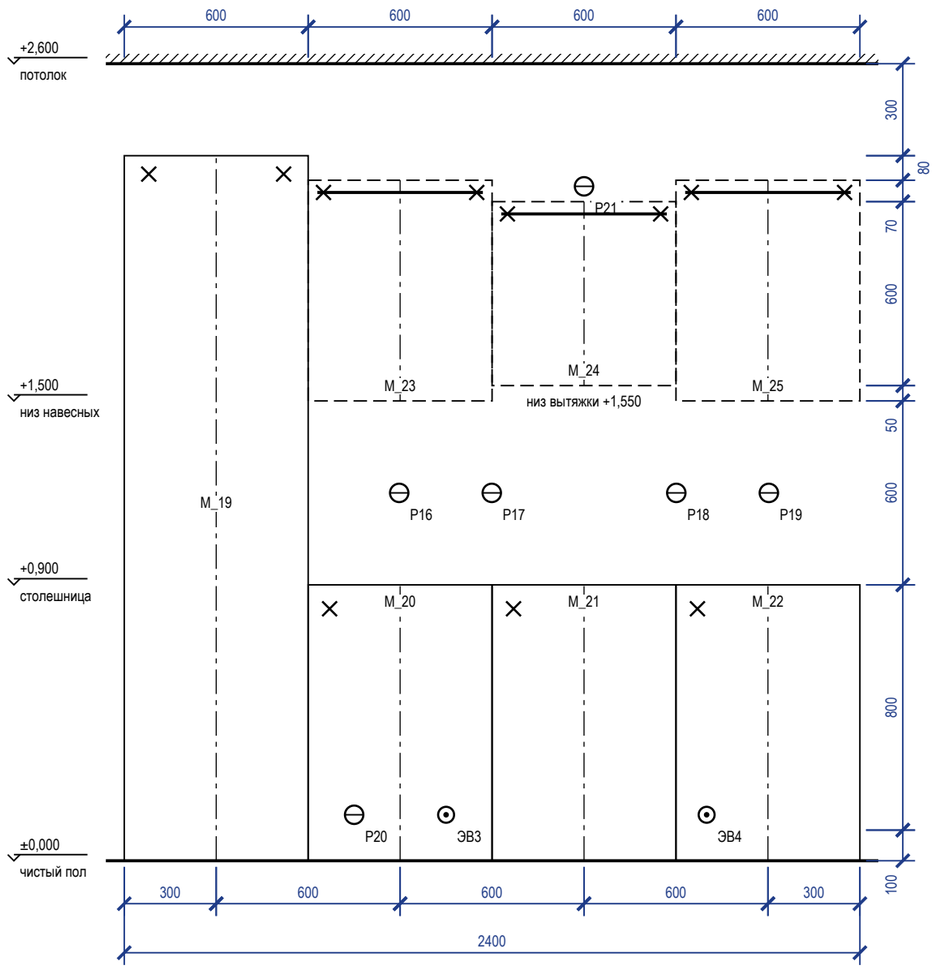


## План столешницы

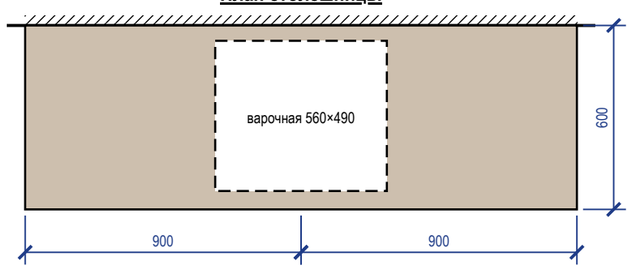


## Привязка выводов к осям модулей

| Код | Назначение | Модуль | От оси, мм | H, мм | Размещение |
|---|---|---|---|---|---|
| P20 | розетка — холодильник встроенный M_19 (розетка в модуле M_20) | M_20 | −150 | 150 | в соседнем модуле, за ящиком |
| P16 | розетка ×2 — фартук: мелкая техника | M_20 | −3 | 1200 | над столешницей (фартук) |
| ЭВ3 | вывод кабеля — варочная панель M_21 | M_20 | +150 | 150 | в соседнем модуле, за ящиком |
| P17 | розетка ×2 — фартук: мелкая техника | M_20 | +299 | 1200 | над столешницей (фартук) |
| P21 | розетка — вытяжка M_24 (в модуле, съёмная панель) | M_24 | 0 | 2200 | в навесном модуле |
| P18 | розетка ×2 — фартук: мелкая техника | M_21 | +301 | 1200 | над столешницей (фартук) |
| ЭВ4 | вывод кабеля — духовой шкаф M_21 (вывод в соседнем модуле M_22) | M_22 | −200 | 150 | в соседнем модуле, за ящиком |
| P19 | розетка ×2 — фартук: мелкая техника | M_22 | +3 | 1200 | над столешницей (фартук) |

## Зазоры под отделку

| Поверхность | Отделка | Зазор, мм | Учесть |
|---|---|---|---|
| фартук | керамогранит | 10 | от чернового основания до корпуса навесных и столешницы |
| стены | окраска | 5 | под штукатурку и шпаклёвку за пеналом |
| пол | инженерная доска | | цоколь — после укладки пола, опоры ±20 мм |

## Условные обозначения


- нижний модуль, пенал (контур)
- невидимый контур: навесной модуль, корпус под столешницей
- ось модуля (от неё — привязка вывода)
- анкер / уголок крепления к стене
- розетка на стене
- вывод кабеля к технике
- B1 — вывод воды B1 / Т3, канализации К1

## Примечания

1. Выводы — по проекту электрики и ВК; привязка по горизонтали — от оси модуля (плюс — вправо по виду), по высоте — от чистого пола до оси вывода.
2. Пенал — уголки к стене 2 шт. сверху; нижние модули — стяжками между собой и уголком к стене; ряд выставить по уровню опорами цоколя.
3. Розетки над столешницей — не ниже 150 мм над ней и не за корпусом техники; розетка за ПММ, духовым шкафом и холодильником — только в соседнем модуле или в зоне цоколя с доступом.
4. Столешница — вырезы по шаблонам выбранных моделей мойки и варочной панели; торцы у стены — герметик, пристеночный плинтус.

| | | | | | | |
|---|---|---|---|---|---|---|
| | | | | | Проект: Четырёхкомнатная квартира | **М 1:20** |
| | Лист | № док. | Подпись | Дата | | |
| Дизайнер | Кырлан А.С. | | | 04.11.26 | Кухня (пом. 6). Монтажная схема | Стадия: П; Лист: 8; Листов: 120 |

## Привязка выводов и крепление модулей

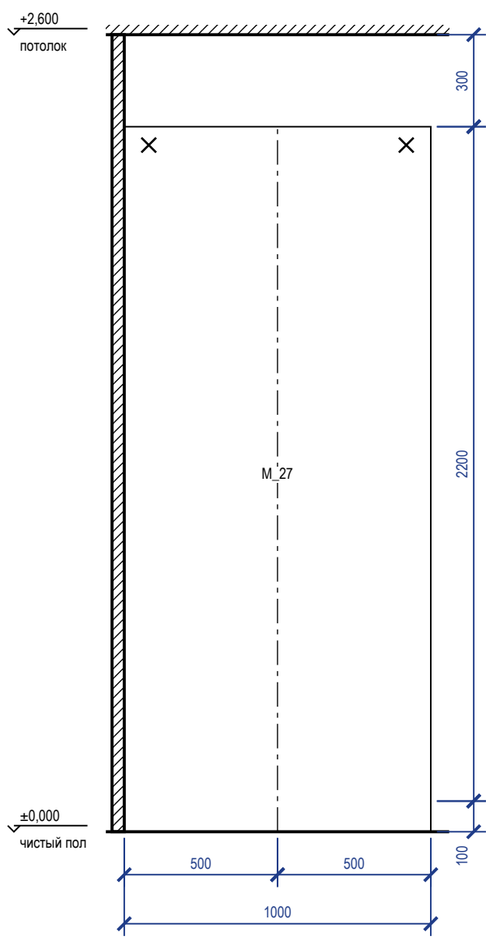


## Привязка выводов к осям модулей

| Код | Назначение | Модуль | От оси, мм | Н, мм | Размещение |
|---|---|---|---|---|---|

## Зазоры под отделку

| Поверхность | Отделка | Зазор, мм | Учесть |
|---|---|---|---|
| фартук | керамогранит | 10 | от чернового основания до корпуса навесных и столешницы |
| стены | окраска | 5 | под штукатурку и шпаклёвку за пеналом |
| пол | инженерная доска | | цоколь — после укладки пола, опоры ±20 мм |

## Условные обозначения


- нижний модуль, пенал (контур)
- ось модуля (от неё — привязка вывода)
- анкер / уголок крепления к стене
- розетка на стене
- вывод кабеля к технике
- B1 — вывод воды B1 / Т3, канализации К1

## Примечания


1. Выводы — по проекту электрики и ВК; привязка по горизонтали — от оси модуля (плюс — вправо по виду), по высоте — от чистого пола до оси вывода.
2. Пенал — уголки к стене 2 шт. сверху; нижние модули — стяжками между собой и уголком к стене; ряд выставить по уровню опорами цоколя.
3. Розетки над столешницей — не ниже 150 мм над ней и не за корпусом техники; розетка за ПММ, духовым шкафом и холодильником — только в соседнем модуле или в зоне цоколя с доступом.
4. Столешница — вырезы по шаблонам выбранных моделей мойки и варочной панели; торцы у стены — герметик, пристеночный плинтус.

| | | | | | |
|---|---|---|---|---|---|
| | | | | | Проект: Четырёхкомнатная квартира — **М 1:20** |
| | Лист | № док. | Подпись | Дата | |
| Дизайнер | Кырлан А.С. | | | 04.11.26 | Кухня (пом. 6). Монтажная схема |
| | | | | | Стадия: П; Лист: 9; Листов: 120 |


### М_07 (пом. 2)

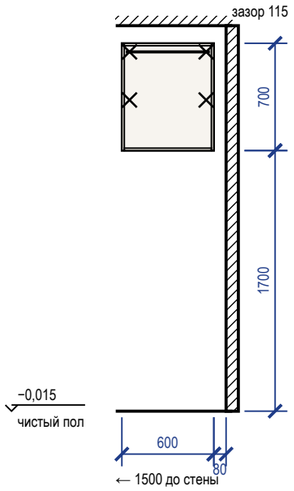



### Система хранения М_08 (пом. 3)

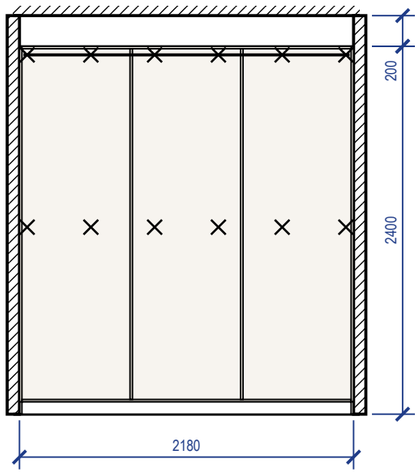



### Система хранения М_09 (пом. 3)

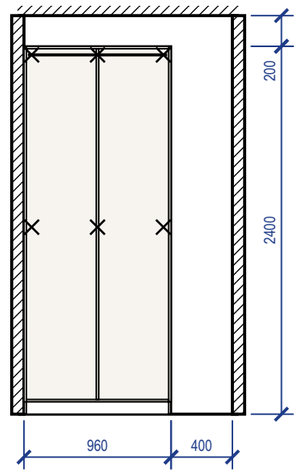


### Шкаф распашной М_15 (пом. 4)

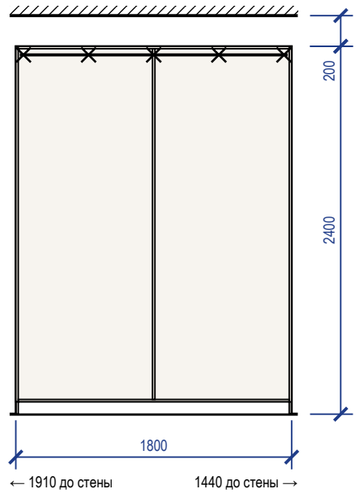


### Система хранения М_17 (пом. 4)

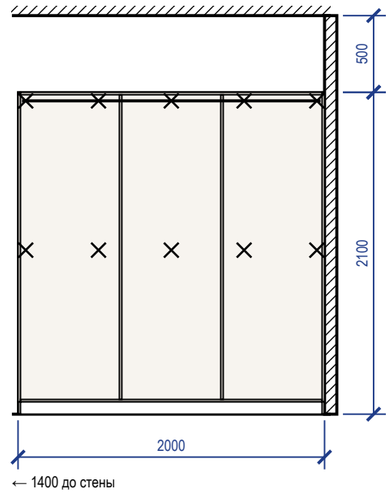


## Крепление и зазоры под отделку (изделия листа 1)

| Марка | Помещение, стена | Основание | Отделка стены | Зазор, мм | Крепёж по планке | От опрокидывания |
|---|---|---|---|---|---|---|
| М_07 | Ванная комната (2), стена Б | по основанию — см. таблицу крепежа | плитка | 10 | анкер 4 шт. (2 ряда) | крепление к стене, 2 точки |
| М_08 | Тёмная комната (3), стена Б | по основанию — см. таблицу крепежа | окраска | 5 | анкер 12 шт. (2 ряда) | крепление к стене, 4 точки |
| М_09 | Тёмная комната (3), стена А | по основанию — см. таблицу крепежа | окраска | 5 | анкер 6 шт. (2 ряда) | крепление к стене, 3 точки |
| М_15 | Детская 1 (4), стена В | по основанию — см. таблицу крепежа | окраска | 5 | анкер 5 шт., шаг 425 | уголок к стене, 3 шт. |
| М_17 | Детская 1 (4), стена Г | по основанию — см. таблицу крепежа | окраска | 5 | анкер 10 шт. (2 ряда) | крепление к стене, 3 точки |

## Крепёж по основанию стены

| Основание стены | Крепёж |
|---|---|
| бетон, ж/б | анкер-шуруп 7,5×72 или дюбель 8×60 с шурупом 5×70 |
| кирпич полнотелый | дюбель 8×80 с шурупом 5×90 |
| газобетон, пазогребень | дюбель для газобетона 10×100 или химический анкер |
| гипсокартон | закладная до обшивки (брус 40×80 или фанера 18 мм), саморез в закладную |

## Условные обозначения


- анкер / уголок крепления к стене
- корпус и полки ЛДСП (вид на стену)
- компенсатор — короб до потолка

## Примечания


1. Установочные размеры — от чистого пола и чистых стен; перед установкой контрольный замер после отделки.
2. Порядок: корпус выставить по уровню опорами цоколя → закрепить к стене по задней планке → навесить двери и фасады, отрегулировать зазоры → подогнать и закрепить компенсатор.
3. Анкеры — с шагом не более 500 мм, не ближе 50 мм от края планки; на ГКЛ только в закладную, установленную до обшивки.
4. Скрытые коммуникации под анкеры проверить детектором; трассы электрики по плану розеток.
5. Монтажная схема на 3 листах, лист 1 из 3; продолжение — на следующем листе схемы. Условные обозначения, таблица крепежа по основанию и примечания повторены на каждом листе.

| | | | | | | |
|---|---|---|---|---|---|---|
| | | | | | Проект: Четырёхкомнатная квартира | М 1:40 |
| | Лист | № док. | Подпись | Дата | | |
| Дизайнер | Кырлан А.С. | | | 04.11.26 | Шкафы. Монтажная схема. Лист 1 из 3 | Стадия: П; Лист: 10; Листов: 120 |


**Система хранения М_18 (пом. 5)**

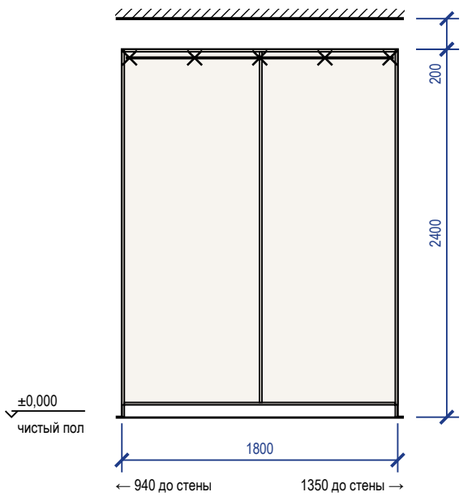



**Шкаф-купе М_28 (пом. 7)**

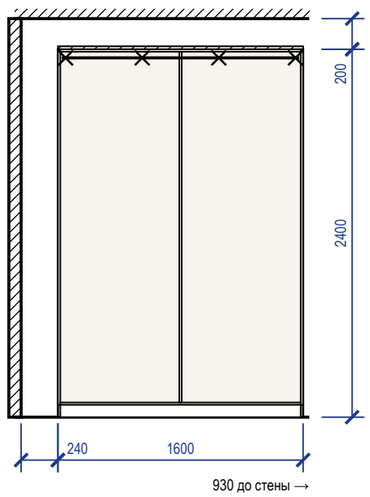



**Система хранения М_31 пом. 8**

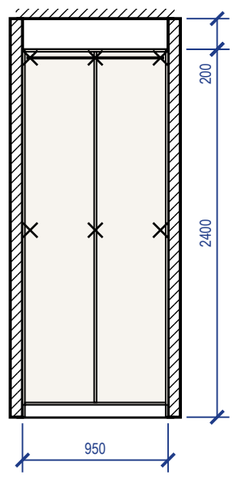


**Система хранения М_32 (пом. 8)**

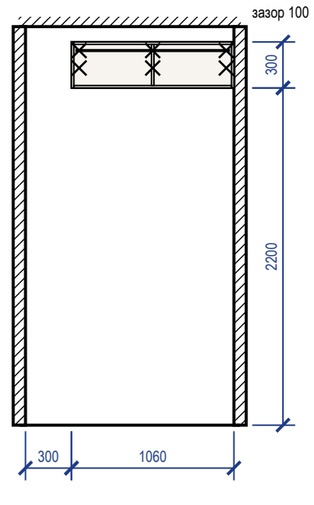


**Шкаф распашной М_34 (пом. 9)**

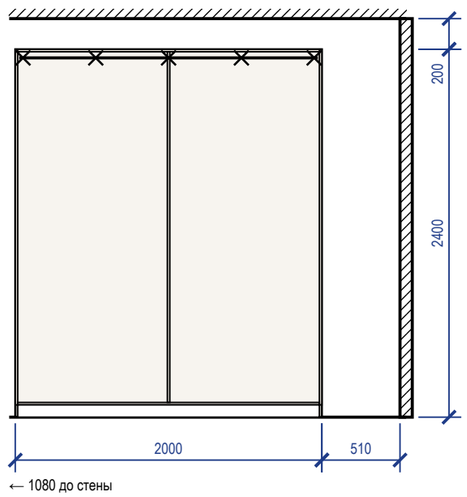


## Крепление и зазоры под отделку (изделия листа 2)

| Марка | Помещение, стена | Основание | Отделка стены | Зазор, мм | Крепёж по планке | От опрокидывания |
|---|---|---|---|---|---|---|
| М_18 | Коридор (5), стена А | по основанию — см. таблицу крепежа | окраска | 5 | анкер 5 шт., шаг 425 | крепление к стене, 4 точки |
| М_28 | Прихожая-коридор (7), стена Б | по основанию — см. таблицу крепежа | окраска | 5 | анкер 4 шт., шаг 500 | крепление к стене, 3 точки |
| М_31 | Гардеробная 2 (8), стена Б | по основанию — см. таблицу крепежа | окраска | 5 | анкер 6 шт. (2 ряда) | крепление к стене, 3 точки |
| М_32 | Гардеробная 2 (8), стена В | по основанию — см. таблицу крепежа | окраска | 5 | анкер 6 шт. (2 ряда) | крепление к стене, 4 точки |
| М_34 | Детская 2 (9), стена А | по основанию — см. таблицу крепежа | окраска | 5 | анкер 5 шт., шаг 475 | уголок к стене, 3 шт. |

## Крепёж по основанию стены

| Основание стены | Крепёж |
|---|---|
| бетон, ж/б | анкер-шуруп 7,5×72 или дюбель 8×60 с шурупом 5×70 |
| кирпич полнотелый | дюбель 8×80 с шурупом 5×90 |
| газобетон, пазогребень | дюбель для газобетона 10×100 или химический анкер |
| гипсокартон | закладная до обшивки (брус 40×80 или фанера 18 мм), саморез в закладную |

## Условные обозначения


- анкер / уголок крепления к стене
- корпус и полки ЛДСП (вид на стену)
- компенсатор — короб до потолка

## Примечания


1. Установочные размеры — от чистого пола и чистых стен; перед установкой контрольный замер после отделки.
2. Порядок: корпус выставить по уровню опорами цоколя → закрепить к стене по задней планке → навесить двери и фасады, отрегулировать зазоры → подогнать и закрепить компенсатор.
3. Анкеры — с шагом не более 500 мм, не ближе 50 мм от края планки; на ГКЛ только в закладную, установленную до обшивки.
4. Скрытые коммуникации под анкеры проверить детектором; трассы электрики по плану розеток.
5. Монтажная схема на 3 листах, лист 2 из 3; продолжение — на следующем листе схемы. Условные обозначения, таблица крепежа по основанию и примечания повторены на каждом листе.

| | | | | | | |
|---|---|---|---|---|---|---|
| | | | | | Проект: Четырёхкомнатная квартира | М 1:40 |
| | Лист | № док. | Подпись | Дата | | |
| Дизайнер | Кырлан А.С. | | | 04.11.26 | Шкафы. Монтажная схема. Лист 2 из 3 | Стадия: П; Лист: 11; Листов: 120 |


**Система хранения М_38 (пом. 12)**

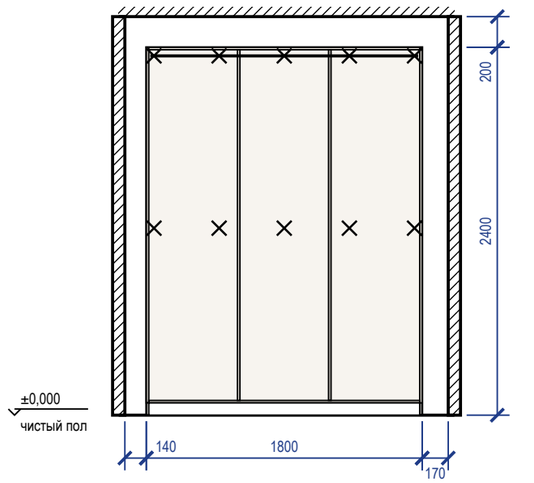


**Система хранения М_39 пом. 13**

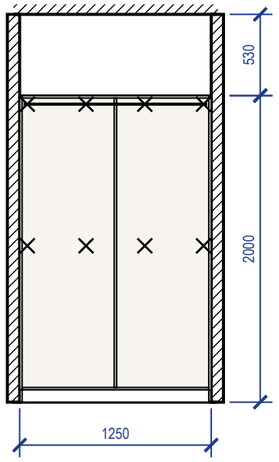


**Система хранения М_40 пом. 13**

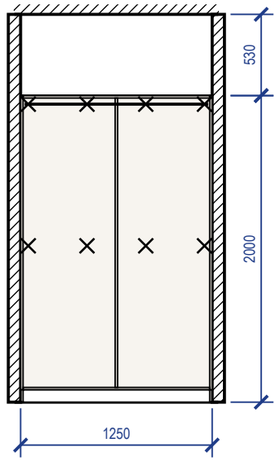


## Крепление и зазоры под отделку (изделия листа 3)

| Марка | Помещение, стена | Основание | Отделка стены | Зазор, мм | Крепёж по планке | От опрокидывания |
|---|---|---|---|---|---|---|
| М_38 | Гардеробная 1 (12), стена Б | по основанию — см. таблицу крепежа | окраска | 5 | анкер 10 шт. (2 ряда) | крепление к стене, 4 точки |
| М_39 | Балкон 1 (13), стена Б | по основанию — см. таблицу крепежа | окраска | 5 | анкер 8 шт. (2 ряда) | крепление к стене, 3 точки |
| М_40 | Балкон 1 (13), стена Г | по основанию — см. таблицу крепежа | окраска | 5 | анкер 8 шт. (2 ряда) | крепление к стене, 3 точки |

## Крепёж по основанию стены

| Основание стены | Крепёж |
|---|---|
| бетон, ж/б | анкер-шуруп 7,5×72 или дюбель 8×60 с шурупом 5×70 |
| кирпич полнотелый | дюбель 8×80 с шурупом 5×90 |
| газобетон, пазогребень | дюбель для газобетона 10×100 или химический анкер |
| гипсокартон | закладная до обшивки (брус 40×80 или фанера 18 мм), саморез в закладную |


## Условные обозначения

- анкер / уголок крепления к стене
- корпус и полки ЛДСП (вид на стену)
- компенсатор — короб до потолка

## Примечания

1. Установочные размеры — от чистого пола и чистых стен; перед установкой контрольный замер после отделки.
2. Порядок: корпус выставить по уровню опорами цоколя → закрепить к стене по задней планке → навесить двери и фасады, отрегулировать зазоры → подогнать и закрепить компенсатор.
3. Анкеры — с шагом не более 500 мм, не ближе 50 мм от края планки; на ГКЛ только в закладную, установленную до обшивки.
4. Скрытые коммуникации под анкеры проверить детектором; трассы электрики по плану розеток.
5. Монтажная схема на 3 листах, лист 3 из 3. Условные обозначения, таблица крепежа по основанию и примечания повторены на каждом листе.

| | | | | | | |
|---|---|---|---|---|---|---|
| | | | | | Проект: Четырёхкомнатная квартира | **М 1:40** |
| | Лист | № док. | Подпись | Дата | | |
| Дизайнер | Кырлан А.С. | | | 04.11.26 | Шкафы. Монтажная схема. Лист 3 из 3 | Стадия: П; Лист: 12; Листов: 120 |

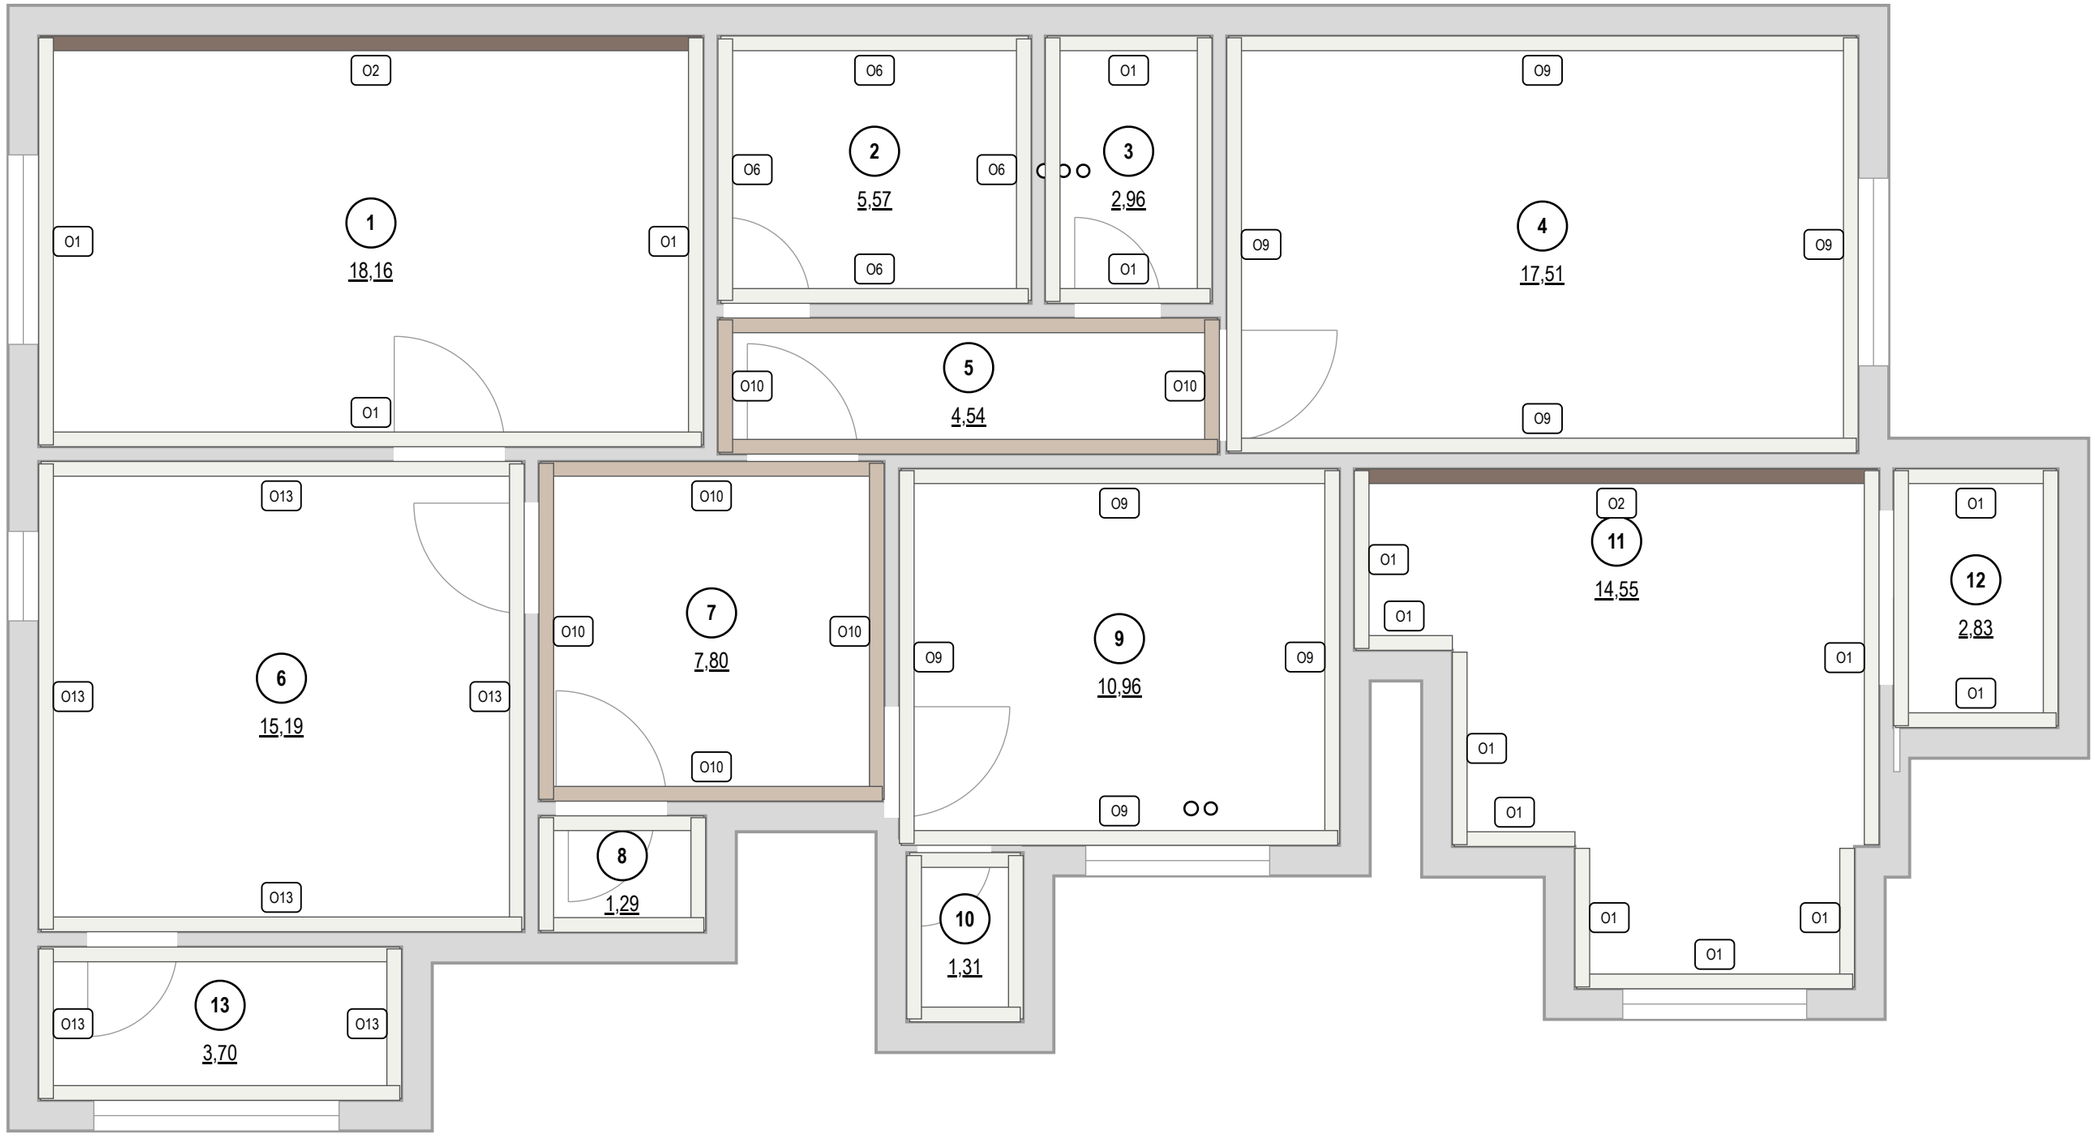


## Покрытия стен

| Марка | Покрытие | Помещение: S, м² | Итого, м² |
|---|---|---|---|
| O1 | окраска Tikkurila · F497 «Paper» | 1: 27,2; 3: 16,6; 8: 8,3; 11: 27,0; 12: 14,6 | 93,8 |
| O2 | окраска Tikkurila · L481 «Silhouette» | 1: 13,5; 11: 11,1 | 24,5 |
| O6 | облицовка плиткой · «тон Paper F497» 600×600 мм | 2: 21,9; 10: 10,0 | 31,8 |
| O9 | окраска Tikkurila · F497 «Paper» | 4: 40,1; 9: 29,1 | 69,3 |
| O10 | окраска Tikkurila · J484 «Castle» | 5: 20,0; 7: 20,0 | 40,0 |
| O13 | окраска Tikkurila · F497 «Paper» | 6: 32,9; 13: 16,4 | 49,3 |

Площади — нетто, по развёрткам (за вычетом проёмов и фартука); высоты помещений — от чистого пола.

| | | | | |
|---|---|---|---|---|
| | | | | |
| | | | | |
| | Лист | № док. | Подпись | Дата |
| Дизайнер | Кырлан А.С. | | | 04.11.26 |
| | | | | |

Проект: Четырёхкомнатная квартира — **М 1:50**

Карта покрытий стен

| Стадия | Лист | Листов |
|---|---|---|
| П | 13 | 120 |

## Колерная карта по помещениям

| Помещение | Поверхность | Образец | Поз. | Система и код цвета | Производитель, линейка / материал, артикул | Блеск | Класс истирания | LRV | Площадь |
|---|---|---|---|---|---|---|---|---|---|
| **1. Зал** 18,16 м² | стены | | **К1** | Tikkurila F497 | Tikkurila · Optiva 5 Matt | матовая | 2 | 88 | 25,9 м² |
| | акцент А | | **К2** | Tikkurila L481 | Tikkurila · Optiva 5 Matt | матовая | 2 | 18 | 13,6 м² |
| | потолок | | **К3** | Tikkurila F497 | Tikkurila · Anti-Reflex 2 | глубокомат. | 2 | 88 | 18,2 м² |
| | пол | | **КМ1** | по образцу | инженерная доска · аналог по хар. | | | | 18,2 м² |
| | плинтус | | **К4** | Tikkurila F497 | МДФ · в цвет Tikkurila | полуглянц. | 2 | 88 | 16,6 м |
| **2. Ванная комната** 5,57 м² | стены | | **КМ2** | тон Paper F497 (тёплый белый) | плитка · аналог по хар. | | | | 22,3 м² |
| | потолок | | **К5** | Tikkurila F497 | Tikkurila · Luja 7 | матовая | 1 | 88 | 5,6 м² |
| | пол | | **КМ3** | тон Castle J484 (тёплый песочный) | керамогранит · аналог по хар. | | | | 5,6 м² |
| **3. Тёмная комната** 2,96 м² | стены | | **К1** | Tikkurila F497 | Tikkurila · Optiva 5 Matt | матовая | 2 | 88 | 16,9 м² |
| | потолок | | **К3** | Tikkurila F497 | Tikkurila · Anti-Reflex 2 | глубокомат. | 2 | 88 | 3,0 м² |
| | пол | | **КМ1** | по образцу | инженерная доска · аналог по хар. | | | | 3,0 м² |
| | плинтус | | **К4** | Tikkurila F497 | МДФ · в цвет Tikkurila | полуглянц. | 2 | 88 | 6,4 м |
| **4. Детская 1** 17,51 м² | стены | | **К6** | Tikkurila F497 | Tikkurila · Joker | полуматов. | 2 | 88 | 40,1 м² |
| | потолок | | **К3** | Tikkurila F497 | Tikkurila · Anti-Reflex 2 | глубокомат. | 2 | 88 | 17,5 м² |
| | пол | | **КМ1** | по образцу | инженерная доска · аналог по хар. | | | | 17,5 м² |
| | плинтус | | **К4** | Tikkurila F497 | МДФ · в цвет Tikkurila | полуглянц. | 2 | 88 | 16,2 м |
| **5. Коридор** 4,54 м² | стены | | **К7** | Tikkurila J484 | Tikkurila · Optiva 20 Semimatt | полуматов. | 2 | 55 | 22,2 м² |
| | потолок | | **К3** | Tikkurila F497 | Tikkurila · Anti-Reflex 2 | глубокомат. | 2 | 88 | 4,5 м² |
| | пол | | **КМ4** | тон Claystone V486 (грейж) | керамогранит · аналог по хар. | | | | 4,5 м² |
| | плинтус | | **К8** | Tikkurila J484 | МДФ · в цвет Tikkurila | полуглянц. | 2 | 55 | 8,1 м |
| **6. Кухня** 15,19 м² | стены | | **К9** | Tikkurila F497 | Tikkurila · Luja 7 | полуматов. | 1 | 88 | 34,5 м² |
| | потолок | | **К5** | Tikkurila F497 | Tikkurila · Luja 7 | матовая | 1 | 88 | 15,2 м² |
| | пол | | **КМ1** | по образцу | инженерная доска · аналог по хар. | | | | 15,2 м² |
| | плинтус | | **К4** | Tikkurila F497 | МДФ · в цвет Tikkurila | полуглянц. | 2 | 88 | 13,8 м |
| | фартук | | **КМ5** | тон Paper F497 (тёплый белый) | керамогранит · аналог по хар. | | | | 1,1 м² |

## Схема палитры проекта

Стиль: Современный (контемпорари) · схема: аналоговая

| основной | основной | второстепенный | акцентный |
|---|---|---|---|
| **Tikkurila F497** | **Tikkurila J484** | **Tikkurila V486** | **Tikkurila L481** |
| Paper<br>LRV 88<br>стены 1,3,4,6,8,9,11,12,13;<br>потолок<br>1,2,3,4,5,6,7,8,9,10,11,12,13;<br>плинтус 1,3,4,6,8,9,11,12; текстиль/декор 1 | Castle<br>LRV 55<br>стены 5,7; плинтус 5,7;<br>текстиль/декор 1,6 | Claystone<br>LRV 44<br>текстиль/декор 1,13 | Silhouette<br>LRV 18<br>акцент 1,11; текстиль/декор<br>1,11 |

План 60/30/10

| 60% | 30% | 10% |
|---|---|---|

Окраска, факт — по площади стен, акцентов, потолков

| 94% | 6% |
|---|---|

окрашено всего 391,5 м²; второстепенный тон несут мебель и текстиль

**Текстиль и декор в цветах вне палитры проекта**

- NCS S 3005-Y20R тёплый тауп-серый — пом. 1 (Т3), 7 (Т15), 9 (Т18)
- Tikkurila H487 Pumice — пом. 1 (Т4), 4 (Т9, Т10, Т11), 9 (Т17, Т19)
- Tikkurila V484 Driftwood — пом. 4 (Т8), 9 (Т16), 13 (Т23)
- NCS S 5010-B10G серо-петроль — пом. 4 (Т12, Т13)
- Farrow & Ball No. 47 Green Smoke — пом. 9 (Т20, Т21)

## Условные обозначения

- **К1** Tikkurila F497 · Paper · Optiva 5 Matt · матовая · кл. 2
- **К2** Tikkurila L481 · Silhouette · Optiva 5 Matt · матовая · кл. 2
- **К3** Tikkurila F497 · Paper · Anti-Reflex 2 · глубокомат. · кл. 2
- **К4** Tikkurila F497 · Paper · МДФ · полуглянц. · кл. 2
- **К5** Tikkurila F497 · Paper · Luja 7 · матовая · кл. 1
- **К6** Tikkurila F497 · Paper · Joker · полуматов. · кл. 2
- **К7** Tikkurila J484 · Castle · Optiva 20 Semimatt · полуматов. · кл. 2
- **К8** Tikkurila J484 · Castle · МДФ · полуглянц. · кл. 2
- **К9** Tikkurila F497 · Paper · Luja 7 · полуматов. · кл. 1
- дерево (доска, паркет, ламинат) — рисунок досок
- керамогранит, плитка, камень — сетка швов по формату

- **КМ1** инженерная доска · аналог: дуб натуральный брашированный, масло-воск, 14/4 мм
- **КМ2** плитка · аналог: керамогранит матовый, тон F497, 600×600×9 мм
- **КМ3** аналог: керамогранит матовый R10, тон J484, 600×600×10 мм
- **КМ4** аналог: керамогранит матовый R10, тон V486, 600×600×10 мм
- **КМ5** аналог: керамогранит матовый, тон F497, 600×600×9 мм
- **КМ6** аналог: керамогранит матовый R11, тон V486, 600×600×10 мм
- **КМ7** керамогранит · аналог: плинтус из керамогранита пола, подрезка 80 мм, верхняя кромка с запилом 45°

К — краска, КМ — отделочный материал (тон КМ — по описанию, эталон — образец материала); кл. — класс истирания (1 — самый стойкий к мытью); LRV — светлота цвета: 0 — чёрный, 100 — белый

## Примечания

1. Цвет на листе и на экране — ориентир. До покраски — выкрас на объекте: не меньше А3 (или лист ГКЛ), на грунте под эту краску, не на белой шпаклёвке, в 2 слоя; на обороте — код, бренд, веер, дата. Смотреть днём и вечером, рядом с образцами пола и плитки. Красить только в цвет утверждённого выкраса.
2. Краску заказывать по коду из графы «Система и код цвета» у бренда этого кода, не «аналогом» другого; весь объём одного кода — одной партией, колеруемую краску — за один проход машины.
3. Площади — те же, что в ведомости отделки (лист С1); сколько краски заказать — в спецификации отделочных материалов (лист С4).
4. Колерная карта на 2 листах: обозначения — на каждом, схема и палитра — на первом, выкрасы — на последнем.

| | | | | | |
|---|---|---|---|---|---|
| | | | | | Проект: Четырёхкомнатная квартира |
| | Лист | № док. | Подпись | Дата | |
| Дизайнер | Кырлан А.С. | | | 04.11.26 | Колерная карта |

| Стадия | Лист | Листов |
|---|---|---|
| П | 14 | 120 |

## Колерная карта по помещениям (продолжение)

| Помещение | Поверхность | Образец | Поз. | Система и код цвета | Производитель, линейка / материал, артикул | Блеск | Класс истирания | LRV | Площадь |
|---|---|---|---|---|---|---|---|---|---|
| **7. Прихожая-коридор** 7,8 м² | стены | | **K7** | Tikkurila J484 | Tikkurila · Optiva 20 Semimatt | полуматов. | 2 | 55 | 23,8 м² |
| | потолок | | **K3** | Tikkurila F497 | Tikkurila · Anti-Reflex 2 | глубокомат. | 2 | 88 | 7,8 м² |
| | пол | | **KM4** | тон Claystone V486 (грейж) | керамогранит · аналог по хар. | | | | 7,8 м² |
| | плинтус | | **K8** | Tikkurila J484 | МДФ · в цвет Tikkurila | полуглянц. | 2 | 55 | 8,7 м |
| **8. Гардеробная 2** 1,29 м² | стены | | **K1** | Tikkurila F497 | Tikkurila · Optiva 5 Matt | матовая | 2 | 88 | 8,7 м² |
| | потолок | | **K3** | Tikkurila F497 | Tikkurila · Anti-Reflex 2 | глубокомат. | 2 | 88 | 1,3 м² |
| | пол | | **KM1** | по образцу | инженерная доска · аналог по хар. | | | | 1,3 м² |
| | плинтус | | **K4** | Tikkurila F497 | МДФ · в цвет Tikkurila | полуглянц. | 2 | 88 | 3,3 м |
| **9. Детская 2** 10,96 м² | стены | | **K6** | Tikkurila F497 | Tikkurila · Joker | полуматов. | 2 | 88 | 29,1 м² |
| | потолок | | **K3** | Tikkurila F497 | Tikkurila · Anti-Reflex 2 | глубокомат. | 2 | 88 | 11,0 м² |
| | пол | | **KM1** | по образцу | инженерная доска · аналог по хар. | | | | 11,0 м² |
| | плинтус | | **K4** | Tikkurila F497 | МДФ · в цвет Tikkurila | полуглянц. | 2 | 88 | 11,8 м |
| **10. Санузел** 1,31 м² | стены | | **KM2** | тон Paper F497 (тёплый белый) | плитка · аналог по хар. | | | | 10,5 м² |
| | потолок | | **K5** | Tikkurila F497 | Tikkurila · Luja 7 | матовая | 1 | 88 | 1,3 м² |
| | пол | | **KM3** | тон Castle J484 (тёплый песочный) | керамогранит · аналог по хар. | | | | 1,3 м² |
| **11. Гостиная** 14,55 м² | стены | | **K1** | Tikkurila F497 | Tikkurila · Optiva 5 Matt | матовая | 2 | 88 | 27,8 м² |
| | акцент А | | **K2** | Tikkurila L481 | Tikkurila · Optiva 5 Matt | матовая | 2 | 18 | 11,1 м² |
| | потолок | | **K3** | Tikkurila F497 | Tikkurila · Anti-Reflex 2 | глубокомат. | 2 | 88 | 14,6 м² |
| | пол | | **KM1** | по образцу | инженерная доска · аналог по хар. | | | | 14,6 м² |
| | плинтус | | **K4** | Tikkurila F497 | МДФ · в цвет Tikkurila | полуглянц. | 2 | 88 | 15,6 м |
| **12. Гардеробная 1** 2,83 м² | стены | | **K1** | Tikkurila F497 | Tikkurila · Optiva 5 Matt | матовая | 2 | 88 | 15,0 м² |
| | потолок | | **K3** | Tikkurila F497 | Tikkurila · Anti-Reflex 2 | глубокомат. | 2 | 88 | 2,8 м² |
| | пол | | **KM1** | по образцу | инженерная доска · аналог по хар. | | | | 2,8 м² |
| | плинтус | | **K4** | Tikkurila F497 | МДФ · в цвет Tikkurila | полуглянц. | 2 | 88 | 5,5 м |
| **13. Балкон 1** 3,7 м² | стены | | **K9** | Tikkurila F497 | Tikkurila · Luja 7 | полуматов. | 1 | 88 | 16,5 м² |
| | потолок | | **K5** | Tikkurila F497 | Tikkurila · Luja 7 | матовая | 1 | 88 | 3,7 м² |
| | пол | | **KM6** | тон Claystone V486 (грейж) | керамогранит · аналог по хар. | | | | 3,7 м² |
| | плинтус | | **KM7** | тон Claystone V486 (грейж) | керамогранит · аналог по хар. | | | | 7,7 м |

## Условные обозначения

- **K1** Tikkurila F497 · Paper · Optiva 5 Matt · матовая · кл. 2
- **K2** Tikkurila L481 · Silhouette · Optiva 5 Matt · матовая · кл. 2
- **K3** Tikkurila F497 · Paper · Anti-Reflex 2 · глубокомат. · кл. 2
- **K4** Tikkurila F497 · Paper · МДФ · полуглянц. · кл. 2
- **K5** Tikkurila F497 · Paper · Luja 7 · матовая · кл. 1
- **K6** Tikkurila F497 · Paper · Joker · полуматов. · кл. 2
- **K7** Tikkurila J484 · Castle · Optiva 20 Semimatt · полуматов. · кл. 2
- **K8** Tikkurila J484 · Castle · МДФ · полуглянц. · кл. 2
- **K9** Tikkurila F497 · Paper · Luja 7 · полуматов. · кл. 1
- дерево (доска, паркет, ламинат) — рисунок досок
- керамогранит, плитка, камень — сетка швов по формату

- **KM1** инженерная доска · аналог: дуб натуральный брашированный, масло-воск, 14/4 мм
- **KM2** плитка · аналог: керамогранит матовый, тон F497, 600×600×9 мм
- **KM3** аналог: керамогранит матовый R10, тон J484, 600×600×10 мм
- **KM4** аналог: керамогранит матовый R10, тон V486, 600×600×10 мм
- **KM5** аналог: керамогранит матовый, тон F497, 600×600×9 мм
- **KM6** аналог: керамогранит матовый R11, тон V486, 600×600×10 мм
- **KM7** керамогранит · аналог: плинтус из керамогранита пола, подрезка 80 мм, верхняя кромка с запилом 45°

К — краска, KM — отделочный материал (тон KM — по описанию, эталон — образец материала); кл. — класс истирания (1 — самый стойкий к мытью); LRV — светлота цвета: 0 — чёрный, 100 — белый

## Перечень выкрасов на согласование

| № | Код | Бренд / веер | Пом. / стена | Подложка | Формат | Статус |
|---|---|---|---|---|---|---|
| 1 | F497 | Tikkurila Symphony / Feel the Colour | 1 | ГКЛ, загрунтованный под эту краску | 600×1000 | на согласов. |
| 2 | G503 | Tikkurila Symphony / Feel the Colour | 1 | ГКЛ, загрунтованный под эту краску | 600×1000 | на согласов. |
| 3 | G497 | Tikkurila Symphony / Feel the Colour | 1 | ГКЛ, загрунтованный под эту краску | 600×1000 | на согласов. |
| 4 | L481 | Tikkurila Symphony / Feel the Colour | 1 A | ГКЛ, загрунтованный под эту краску | 600×1000 | на согласов. |
| 5 | V477 | Tikkurila Symphony / Feel the Colour | 1 A | ГКЛ, загрунтованный под эту краску | 600×1000 | на согласов. |
| 6 | L462 | Tikkurila Symphony / Feel the Colour | 1 A | ГКЛ, загрунтованный под эту краску | 600×1000 | на согласов. |
| 7 | J484 | Tikkurila Symphony / Feel the Colour | 5 | ГКЛ, загрунтованный под эту краску | 600×1000 | на согласов. |
| 8 | X487 | Tikkurila Symphony / Feel the Colour | 5 | ГКЛ, загрунтованный под эту краску | 600×1000 | на согласов. |
| 9 | X463 | Tikkurila Symphony / Feel the Colour | 5 | ГКЛ, загрунтованный под эту краску | 600×1000 | на согласов. |
| | | | | | | |

… ещё 2 выкрасов — в ведомости отделки


## Примечания

1. Цвет на листе и на экране — ориентир. До покраски — выкрас на объекте: не меньше А3 (или лист ГКЛ), на грунте под эту краску, не на белой шпаклёвке, в 2 слоя; на обороте — код, бренд, веер, дата. Смотреть днём и вечером, рядом с образцами пола и плитки. Красить только в цвет утверждённого выкраса.
2. Краску заказывать по коду из графы «Система и код цвета» у бренда этого кода, не «аналогом» другого; весь объём одного кода — одной партией, колеруемую краску — за один проход машины.
3. Площади — те же, что в ведомости отделки (лист С1); сколько краски заказать — в спецификации отделочных материалов (лист С4).
4. Колерная карта на 2 листах: обозначения — на каждом, схема и палитра — на первом, выкрасы — на последнем.

| | | | | | |
|---|---|---|---|---|---|
| | | | | | Проект: Четырёхкомнатная квартира |
| | Лист | № док. | Подпись | Дата | |
| Дизайнер | Кырлан А.С. | | | 04.11.26 | Колерная карта |

| Стадия | Лист | Листов |
|---|---|---|
| П | 15 | 120 |

выпуск 04.11.2026 № b23f08ad9b · стр. 15 из 120

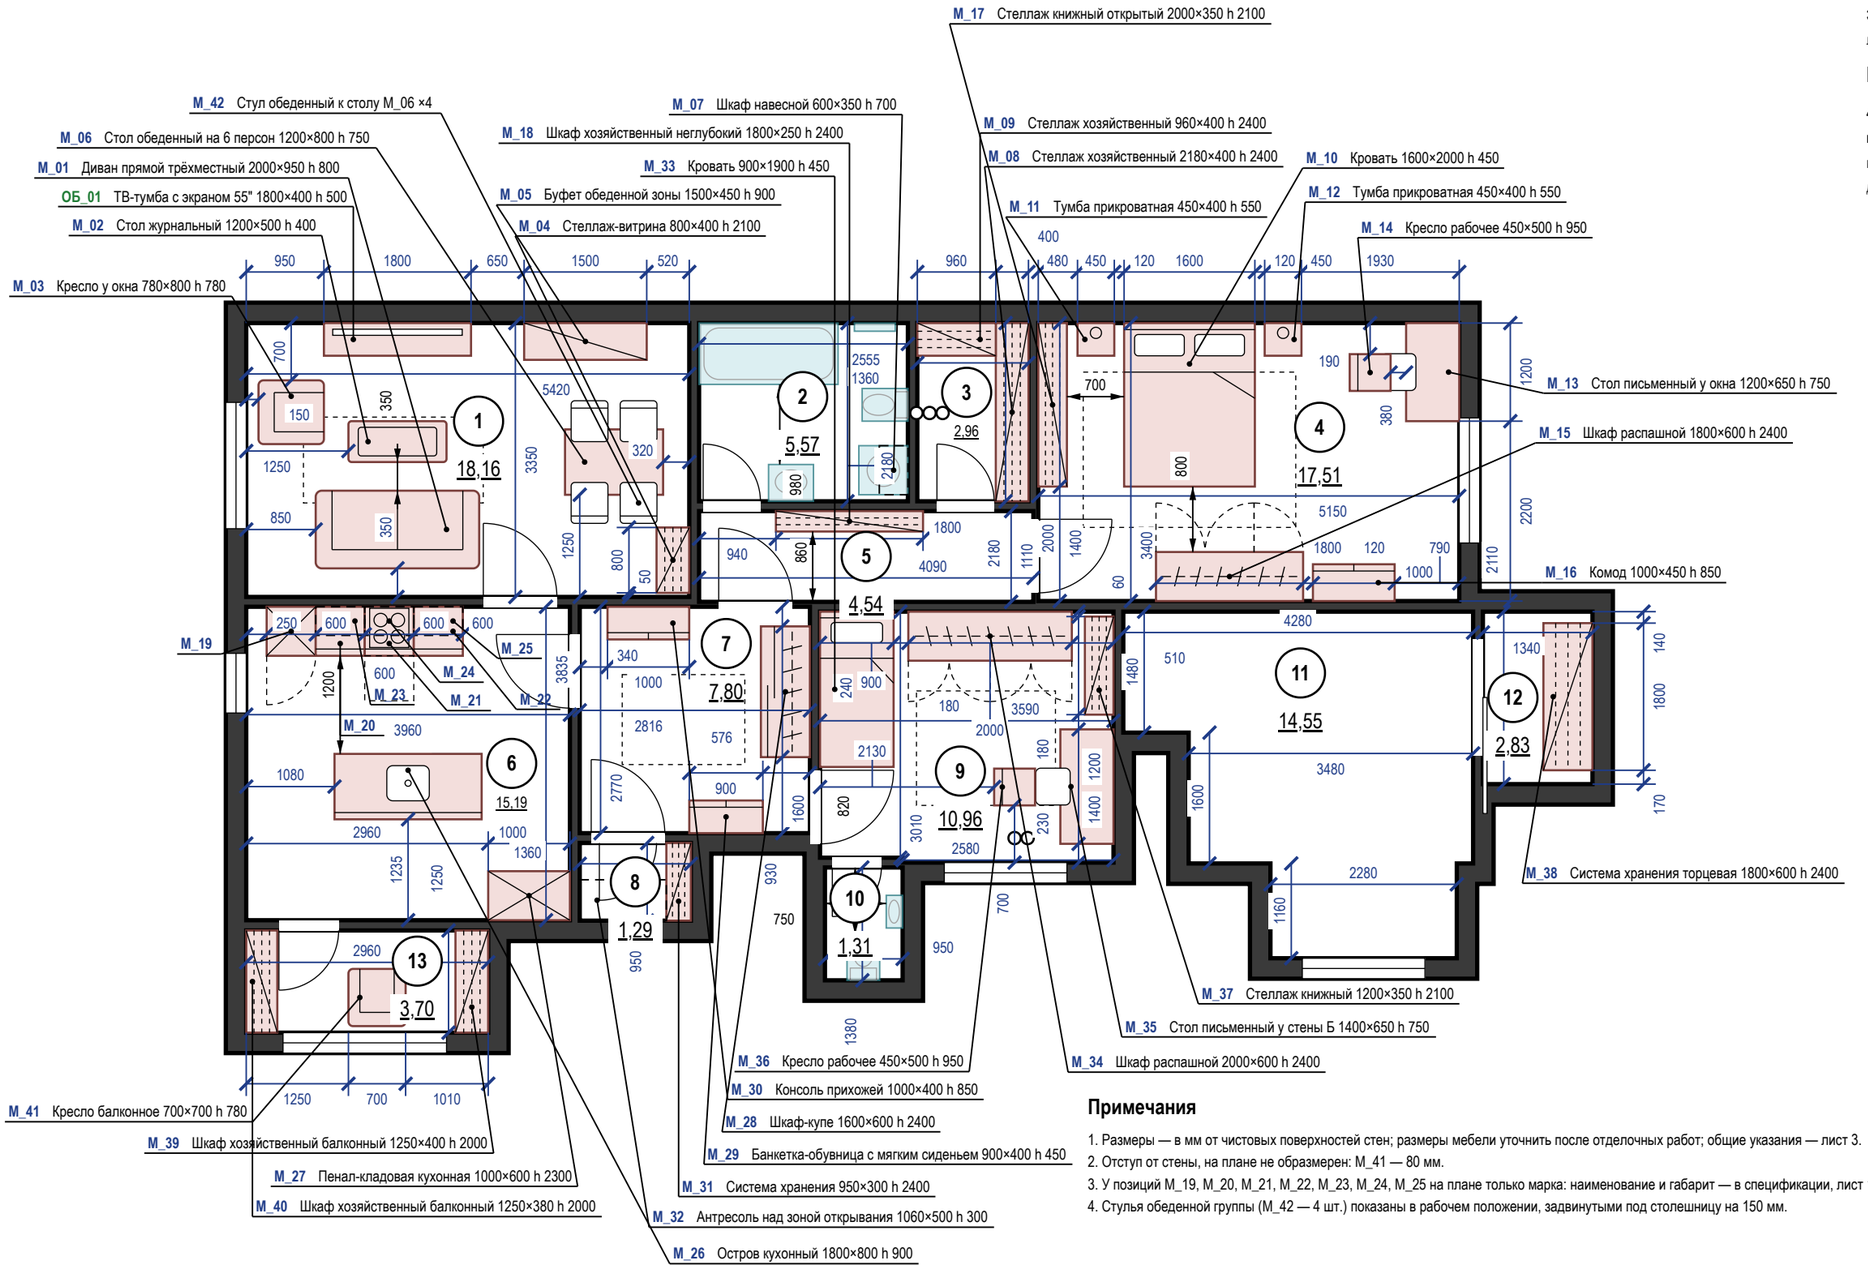


**Экспликация помещений**

лист 6 · на плане — номера в марках

## Ведомость мебели и оборудования

43 позиц. (46 шт.) — не помещается на листе:
полностью на листе 17 «Спецификация мебели и оборудования»
марка, наименование, Ш×Г×В, материал, модель,
допуск замены. Марки на плане — по ней.

## Примечания

1. Размеры — в мм от чистовых поверхностей стен; размеры мебели уточнить после отделочных работ; общие указания — лист 3.
2. Отступ от стены, на плане не образмерен: M_41 — 80 мм.
3. У позиций M_19, M_20, M_21, M_22, M_23, M_24, M_25 на плане только марка: наименование и габарит — в спецификации, лист 17.
4. Стулья обеденной группы (M_42 — 4 шт.) показаны в рабочем положении, задвинутыми под столешницу на 150 мм.

| | | | | | | |
|---|---|---|---|---|---|---|
| | | | | | Проект: Четырёхкомнатная квартира | **М 1:75** |
| | Лист | № док. | Подпись | Дата | План размещения мебели и оборудования | Стадия / Лист / Листов |
| Дизайнер | Кырлан А.С. | | | 04.11.26 | | П / 16 / 120 |

| Поз. | Наименование и техническая характеристика | Тип, марка, обозначение документа, опросного листа | Код продукции | Поставщик | Ед. измерения | Кол. | Масса 1 ед., кг | Примечание |
|---|---|---|---|---|---|---|---|---|
| | **Мебель встроенная и корпусная (изготовление по чертежам мебельщика)** | | | | | | | |
| M_07 | Шкаф навесной над стиральной машиной; каркас и полки — ЛДСП 16 мм, декор «дуб натуральный»; без фасадов; Ш×Г×В 600×350×700 мм | | | изготовление на заказ | шт. | 1 | | пом. 2; крепление к стене |
| M_08 | Стеллаж хозяйственный, 6 полок; каркас и полки — ЛДСП 16 мм, декор «дуб натуральный»; без фасадов; Ш×Г×В 2180×400×2400 мм | | | изготовление на заказ | шт. | 1 | | пом. 3; крепление к стене |
| M_09 | Стеллаж хозяйственный, 6 полок; каркас и полки — ЛДСП 16 мм, декор «дуб натуральный»; без фасадов; Ш×Г×В 960×400×2400 мм | | | изготовление на заказ | шт. | 1 | | пом. 3; крепление к стене |
| M_15 | Шкаф распашной, 3 секции; корпус ЛДСП 16 мм; фасады — МДФ 18 мм, эмаль матовая; цвет фасадов — в цвет стен (Tikkurila F497); Ш×Г×В 1800×600×2400 мм | | | изготовление на заказ | шт. | 1 | | пом. 4; крепление к стене |
| M_17 | Стеллаж книжный открытый; каркас и полки — ЛДСП 16 мм, декор «дуб натуральный»; без фасадов; Ш×Г×В 2000×350×2100 мм | | | изготовление на заказ | шт. | 1 | | пом. 4; крепление к стене |
| M_18 | Шкаф хозяйственный неглубокий; корпус ЛДСП 16 мм; фасады — МДФ 18 мм, эмаль матовая; цвет фасадов — в цвет стен (Tikkurila J484); Ш×Г×В 1800×250×2400 мм | | | изготовление на заказ | шт. | 1 | | пом. 5; крепление к стене |
| M_19 | Пенал кухонный с встроенным холодильником; корпус ЛДСП 16 мм; фасады — МДФ 18 мм, эмаль матовая; цвет фасадов в цвет стен (Tikkurila F497); Ш×Г×В 600×600×2300 мм | | | изготовление на заказ | шт. | 1 | | пом. 6; крепление к стене |
| M_20 | Модуль нижний, ящики; корпус ЛДСП 16 мм; фасады — МДФ 18 мм, эмаль матовая; цвет фасадов — в цвет стен (Tikkurila F497); Ш×Г×В 600×600×900 мм | | | изготовление на заказ | шт. | 1 | | пом. 6 |
| M_21 | Модуль нижний: варочная панель и духовой шкаф; корпус ЛДСП 16 мм; фасады — МДФ 18 мм, эмаль матовая; цвет фасадов — в цвет стен (Tikkurila F497); Ш×Г×В 600×600×900 мм | | | изготовление на заказ | шт. | 1 | | пом. 6 |
| M_22 | Модуль нижний, ящики и бутылочница; корпус ЛДСП 16 мм; фасады — МДФ 18 мм, эмаль матовая; цвет фасадов — в цвет стен (Tikkurila F497); Ш×Г×В 600×600×900 мм | | | изготовление на заказ | шт. | 1 | | пом. 6 |
| M_23 | Модуль навесной, 2 секции; корпус ЛДСП 16 мм; фасады — МДФ 18 мм, эмаль матовая; цвет фасадов — в цвет стен (Tikkurila F497); Ш×Г×В 600×350×720 мм | | | изготовление на заказ | шт. | 1 | | пом. 6 |
| M_24 | Вытяжка встраиваемая в шкаф; корпус ЛДСП 16 мм; фасады — МДФ 18 мм, эмаль матовая; цвет фасадов — в цвет стен (Tikkurila F497); Ш×Г×В 600×350×600 мм | | | изготовление на заказ | шт. | 1 | | пом. 6 |
| M_25 | Модуль навесной, 2 секции; корпус ЛДСП 16 мм; фасады — МДФ 18 мм, эмаль матовая; цвет фасадов — в цвет стен (Tikkurila F497); Ш×Г×В 600×350×720 мм | | | изготовление на заказ | шт. | 1 | | пом. 6 |
| M_26 | Остров кухонный с мойкой и посудомоечной машиной; корпус ЛДСП 16 мм; фасады — МДФ 18 мм, эмаль матовая; цвет фасадов — в цвет стен (Tikkurila F497); Ш×Г×В 1800×800×900 мм | | | изготовление на заказ | шт. | 1 | | пом. 6 |
| M_27 | Пенал-кладовая кухонная; корпус ЛДСП 16 мм; фасады — МДФ 18 мм, эмаль матовая; цвет фасадов — в цвет стен (Tikkurila F497); Ш×Г×В 1000×600×2300 мм | | | изготовление на заказ | шт. | 1 | | пом. 6; крепление к стене |
| M_28 | Шкаф-купе, 3 двери; корпус ЛДСП 16 мм; фасады — ЛДСП 10 мм в алюминиевом профиле; Ш×Г×В 1600×600×2400 мм | | | изготовление на заказ | шт. | 1 | | пом. 7; крепление к стене |
| M_31 | Система хранения: штанга, полки, ящики; каркас и полки — ЛДСП 16 мм, декор «дуб натуральный»; без фасадов; Ш×Г×В 950×300×2400 мм | | | изготовление на заказ | шт. | 1 | | пом. 8; крепление к стене |
| M_32 | Антресоль над зоной открывания двери; каркас и полки — ЛДСП 16 мм, декор «дуб натуральный»; без фасадов; Ш×Г×В 1060×500×300 мм | | | изготовление на заказ | шт. | 1 | | пом. 8; крепление к стене |
| M_34 | Шкаф распашной, 4 секции; корпус ЛДСП 16 мм; фасады — МДФ 18 мм, эмаль матовая; цвет фасадов — в цвет стен (Tikkurila F497); Ш×Г×В 2000×600×2400 мм | | | изготовление на заказ | шт. | 1 | | пом. 9; крепление к стене |
| M_38 | Система хранения торцевая: штанги, полки; каркас и полки — ЛДСП 16 мм, декор «дуб натуральный»; без фасадов; Ш×Г×В 1800×600×2400 мм | | | изготовление на заказ | шт. | 1 | | пом. 12; крепление к стене |
| M_39 | Шкаф хозяйственный балконный; каркас и полки — ЛДСП 16 мм, декор «дуб натуральный»; без фасадов; Ш×Г×В 1250×400×2000 мм | | | изготовление на заказ | шт. | 1 | | пом. 13; крепление к стене |
| M_40 | Шкаф хозяйственный балконный; каркас и полки — ЛДСП 16 мм, декор «дуб натуральный»; без фасадов; Ш×Г×В 1250×380×2000 мм | | | изготовление на заказ | шт. | 1 | | пом. 13; крепление к стене |
| | **Мебель покупная** | | | | | | | |
| M_01 | Диван прямой трёхместный; обивка букле; Ш×Г×В 2000×950×800 мм | диван прямой, глубокая посадка, съёмные чехлы | | аналог по характеристикам | шт. | 1 | | пом. 1; допуск замены Ш 1900–2100, Г ≤ 1000 |

## Примечания

1. Позиции мебели совпадают с марками на плане расстановки; размеры Ш×Г×В — Ш вдоль стены, Г от стены.
2. Размеры и привязки плана расстановки — в мм от чистовых поверхностей стен: слой штукатурки 20 мм по блоку и 5 мм шпаклёвки по ГКЛ учтён; привязки — от стен и углов помещения, а не от другой мебели.
3. План расстановки не является документацией для изготовления мебели. Встроенная и корпусная мебель изготавливается по чертежам мебельщика после контрольного обмера (после штукатурки); «стена в стену» — с зазором 10 мм с каждой стороны или с компенсаторами; графы «Тип, марка» и «Код продукции» для неё не заполняются (ГОСТ 21.110-2013).
4. Покупные изделия — аналог по характеристикам: заменять только на изделия не больше указанного габарита и того же материала и цвета.
5. Материал и цвет, не указанные в данных изделия, приняты по концепции: тон дерева — по полу, обивка — по вторичному цвету палитры; образцы согласовать до заказа.
6. Масса 1 ед. для изделий до 25 кг не указывается. Техника — по монтажным схемам изготовителя; выводы — по листам ЭОМ и ВК.

| | | | | | |
|---|---|---|---|---|---|
| | | | | | Проект: Четырёхкомнатная квартира |
| | Лист | № док. | Подпись | Дата | |
| Дизайнер | Кырлан А.С. | | | 04.11.26 | Спецификация мебели и оборудования |

| Стадия | Лист | Листов |
|---|---|---|
| П | 17 | 120 |

| Поз. | Наименование и техническая характеристика | Тип, марка, обозначение документа, опросного листа | Код продукции | Поставщик | Ед. измерения | Кол. | Масса 1 ед., кг | Примечание |
|---|---|---|---|---|---|---|---|---|
| М_02 | Стол журнальный; дерево — дуб натуральный; Ш×Г×В 1200×500×400 мм | стол журнальный прямоугольный | | аналог по характеристикам | шт. | 1 | | пом. 1; допуск замены Ш 1100–1300 |
| М_03 | Кресло у окна; обивка — ткань, цвет Tikkurila V486; Ш×Г×В 780×800×780 мм | кресло мягкое на деревянных ножках | | аналог по характеристикам | шт. | 1 | | пом. 1; допуск замены Ш 750–850, В ≤ 790 (не выше подоконника) |
| М_04 | Стеллаж-витрина; дерево — дуб натуральный, металл — латунь; Ш×Г×В 800×400×2100 мм | стеллаж открытый, 5 полок | | аналог по характеристикам | шт. | 1 | | пом. 1; крепление к стене; допуск замены Ш 750–850 |
| М_05 | Буфет обеденной зоны; дерево — дуб натуральный, металл — латунь; Ш×Г×В 1500×450×900 мм | буфет 3-дверный | | аналог по характеристикам | шт. | 1 | | пом. 1; крепление к стене; допуск замены Ш 1400–1600, Г ≤ 470 |
| М_06 | Стол обеденный на 6 персон; дерево — дуб натуральный; Ш×Г×В 1200×800×750 мм | стол обеденный прямоугольный, раскладной до 1800 | | аналог по характеристикам | шт. | 1 | | пом. 1; допуск замены Ш 1200–1400 в сложенном виде, Г 800–900 |
| М_42 | Стул обеденный к столу М_06; обивка — ткань, цвет Tikkurila V486; каркас — дуб натуральный; Ш×Г×В 450×500×820 мм | | | аналог по характеристикам | шт. | 4 | | пом. 1; замена ≤ габарита |
| ОБ_01 | ТВ-тумба с экраном 55" диагональ 55"; крепление — настенный кронштейн по паспорту модели; Ш×Г×В 1800×400×500 мм | тумба ТВ подвесная, 3 ящика | | аналог по характеристикам | шт. | 1 | | пом. 1; допуск замены Ш 1700–1900, Г ≤ 450 |
| М_10 | Кровать 1600×2000; мягкое изголовье, обивка — ткань, цвет Tikkurila V486; Ш×Г×В 1600×2000×450 мм | кровать с мягким изголовьем | | аналог по характеристикам | шт. | 1 | | пом. 4; допуск замены Ш 1600, Д 2000–2050 |
| М_11, М_12 | Тумба прикроватная; дерево — дуб натуральный; Ш×Г×В 450×400×550 мм | тумба прикроватная, 2 ящика | | аналог по характеристикам | шт. | 2 | | пом. 4; допуск замены Ш 400–500 |
| М_13 | Стол письменный у окна; дерево — дуб натуральный, металл — чёрный матовый; Ш×Г×В 1200×650×750 мм | стол письменный с тумбой | | аналог по характеристикам | шт. | 1 | | пом. 4; допуск замены Ш 1100–1300, Г 600–700 |
| М_14, М_36 | Кресло рабочее; металл — чёрный матовый; Ш×Г×В 450×500×950 мм | кресло рабочее на роликах | | аналог по характеристикам | шт. | 2 | | пом. 4, 9; допуск замены Ш 480–560 |
| М_16 | Комод, 4 ящика; дерево — дуб натуральный; Ш×Г×В 1000×450×850 мм | комод 4 ящика | | аналог по характеристикам | шт. | 1 | | пом. 4; крепление к стене; допуск замены Ш 950–1100 |
| М_29 | Банкетка-обувница с мягким сиденьем; дерево — дуб натуральный; Ш×Г×В 900×400×450 мм | банкетка-обувница | | аналог по характеристикам | шт. | 1 | | пом. 7; допуск замены Ш 800–950 |
| М_30 | Консоль прихожей, 3 ящика; дерево — дуб натуральный, металл — чёрный матовый; Ш×Г×В 1000×400×850 мм | консоль-комод | | аналог по характеристикам | шт. | 1 | | пом. 7; крепление к стене; допуск замены Ш 950–1100 |
| М_33 | Кровать 900×1900; мягкое изголовье, обивка — ткань, цвет Tikkurila V486; Ш×Г×В 900×1900×450 мм | кровать односпальная с мягким изголовьем | | аналог по характеристикам | шт. | 1 | | пом. 9; допуск замены Ш 900, Д 1900–1950 |
| М_35 | Стол письменный у стены Б, рядом с окном стены В: свет боковой; дерево — дуб натуральный, металл — чёрный матовый; Ш×Г×В 1400×650×750 мм | стол письменный с тумбой | | аналог по характеристикам | шт. | 1 | | пом. 9; допуск замены Ш 1300–1500, Г 600–700 |
| М_37 | Стеллаж книжный; дерево — дуб натуральный; Ш×Г×В 1200×350×2100 мм | | | аналог по характеристикам | шт. | 1 | | пом. 9; крепление к стене; замена ≤ габарита |
| М_41 | Кресло балконное; металл — чёрный матовый; Ш×Г×В 700×700×780 мм | кресло на металлическом каркасе | | аналог по характеристикам | шт. | 1 | | пом. 13; допуск замены Ш 650–750, В ≤ 850 (не выше подоконника) |
| | **Техника встраиваемая и бытовая (покупные изделия), светильники под розетки** | | | | | | | |
| | Стиральная машина встраиваемая, у М_07 | аналог по характеристикам: тип загрузки — по листу ВК, по листу ВК | | по выбору заказчика до изготовления мебели | шт. | 1 | | пом. 2; по схеме изготовителя |
| | Холодильник встраиваемый, в модуле М_19 | аналог по характеристикам: полновстраиваемый под фасад, ниша 1780 × 560 × 550 мм, вентиляция решётка в цоколе, выход сверху | | по выбору заказчика до изготовления мебели | шт. | 1 | | пом. 6; по схеме изготовителя |
| | Духовой шкаф встраиваемый, в модуле М_21 | аналог по характеристикам: 60 см, лицевая панель 595 мм, ниша 560 × 600, глубина ≥ 550 мм, вентиляция за прибором | | по выбору заказчика до изготовления мебели | шт. | 1 | | пом. 6; по схеме изготовителя |

| | | | | | | | |
|---|---|---|---|---|---|---|---|
| | | | | | Проект: Четырёхкомнатная квартира | | |
| | Лист | № док. | Подпись | Дата | Спецификация мебели и оборудования (продолжение) | Стадия | Лист | Листов |
| Дизайнер | Кырлан А.С. | | | 04.11.26 | | П | 18 | 120 |

| Поз. | Наименование и техническая характеристика | Тип, марка, обозначение документа, опросного листа | Код продукции | Поставщик | Ед. измерения | Кол. | Масса 1 ед., кг | Примечание |
|---|---|---|---|---|---|---|---|---|
| | Варочная панель встраиваемая, индукционная, в модуле M_21 | аналог по характеристикам: индукционная 60 см, вырез 560 × 490 мм по шаблону модели | | по выбору заказчика до изготовления мебели | шт. | 1 | | пом. 6; по схеме изготовителя |
| | Вытяжка встраиваемая, в модуле M_24 | аналог по характеристикам: производительность — по расчёту ОВ, шум ≤ 55 дБ(А) | | по выбору заказчика до изготовления мебели | шт. | 1 | | пом. 6; по схеме изготовителя |
| | Посудомоечная машина встраиваемая, в модуле M_26; ниша 600 мм | аналог по характеристикам: полновстраиваемая 60 см под фасад, ниша 600 × по высоте ряда мм, навеска фасада в комплекте | | по выбору заказчика до изготовления мебели | шт. | 1 | | пом. 6; по схеме изготовителя |
| | Торшер, у поз. M_01; абажур — ткань или опаловое стекло; лампа 2700 K | | | аналог по характеристикам | шт. | 1 | | пом. 1; розетка Р3 (ЭОМ) |
| | **Текстиль** | | | | | | | |
| T1 | Портьеры-волна, два полотна; лён 100 %; цвет Tikkurila V486; карниз 2150 мм, высота 2690 мм, сборка 2 | | | аналог по характеристикам | шт. | 2 | | пом. 1 |
| T2 | Тюль-вуаль, одно полотно; полиэстер 100 %; цвет Tikkurila F497; карниз 2150 мм, высота 2690 мм, сборка 2,5 | | | аналог по характеристикам | шт. | 1 | | пом. 1 |
| T3 | Ковёр мягкой группы; шерсть 100 %; цвет NCS S 3005-Y20R; 2200×1050 мм | | | аналог по характеристикам | шт. | 1 | | пом. 1; с подложкой |
| T4 | Подушки декоративные на диван; лён 100 %; цвет Tikkurila H487 | | | аналог по характеристикам | шт. | 3 | | пом. 1 |
| T5 | Подушки декоративные на диван, акцент; хлопковый бархат 100 %; цвет Tikkurila L481 | | | аналог по характеристикам | шт. | 2 | | пом. 1 |
| T6 | Плед на диван; шерсть мериноса 100 %; цвет Tikkurila L481 | | | аналог по характеристикам | шт. | 1 | | пом. 1 |
| T7 | Раннер на обеденный стол; лён 100 %; цвет Tikkurila J484 | | | аналог по характеристикам | шт. | 1 | | пом. 1 |
| T8 | Портьеры стационарные, два полотна; лён 55 %, хлопок 45 %; цвет Tikkurila V484; карниз 2140 мм, высота 2690 мм, сборка 2 | | | аналог по характеристикам | шт. | 2 | | пом. 4 |
| T9 | Римская штора блэкаут: окно закрывает она, стол M_13 у окна не мешает; хлопок 100 %, подкладка полиэстер; цвет Tikkurila H487; карниз 1650 мм, высота 1900 мм | | | аналог по характеристикам | шт. | 1 | | пом. 4 |
| T10 | Ковёр у кровати; шерсть 80 %, хлопок 20 %; цвет Tikkurila H487; 2600×1900 мм | | | аналог по характеристикам | шт. | 1 | | пом. 4; с подложкой |
| T11 | Подушки декоративные на кровать; лён 100 %; цвет Tikkurila H487 | | | аналог по характеристикам | шт. | 2 | | пом. 4 |
| T12 | Подушка декоративная, акцент; хлопковый бархат 100 %; цвет NCS S 5010-B10G | | | аналог по характеристикам | шт. | 1 | | пом. 4 |
| T13 | Плед на кровать; хлопок 100 %; цвет NCS S 5010-B10G | | | аналог по характеристикам | шт. | 1 | | пом. 4 |
| T14 | Рулонная штора кассетная, ткань димаут; полиэстер 100 %; цвет Tikkurila J484; карниз 890 мм, высота 1900 мм | | | аналог по характеристикам | шт. | 1 | | пом. 6 |
| T15 | Ковёр прихожей, низкий ворс; шерсть 80 %, полиамид 20 %; цвет NCS S 3005-Y20R; 1500×1100 мм | | | аналог по характеристикам | шт. | 1 | | пом. 7; с подложкой |
| T16 | Портьеры стационарные, два полотна, до подоконника: радиатор под окном открыт; лён 55 %, хлопок 45 %; цвет Tikkurila V484; карниз 1800 мм, высота 1930 мм, сборка 2 | | | аналог по характеристикам | шт. | 2 | | пом. 9 |
| T17 | Римская штора блэкаут: закрывает проём целиком, радиатор под окном не задевает; хлопок 100 %, подкладка полиэстер; цвет Tikkurila H487; карниз 1620 мм, высота 1900 мм | | | аналог по характеристикам | шт. | 1 | | пом. 9 |
| T18 | Ковёр игровой зоны; шерсть 100 %; цвет NCS S 3005-Y20R; 1700×1400 мм | | | аналог по характеристикам | шт. | 1 | | пом. 9; с подложкой |
| T19 | Подушки декоративные на кровать; лён 100 %; цвет Tikkurila H487 | | | аналог по характеристикам | шт. | 2 | | пом. 9 |
| T20 | Подушка декоративная, акцент; шерсть 60 %, полиэстер 40 %; цвет Farrow & Ball No. 47 | | | аналог по характеристикам | шт. | 1 | | пом. 9 |
| T21 | Плед на кровать; хлопок 100 %; цвет Farrow & Ball No. 47 | | | аналог по характеристикам | шт. | 1 | | пом. 9 |
| T22 | Рулонная штора кассетная, солнцезащитная; полиэстер 100 %; цвет Tikkurila V486; карниз 2140 мм, высота 1700 мм | | | аналог по характеристикам | шт. | 1 | | пом. 13 |
| T23 | Плед на кресло M_41; шерсть 100 %; цвет Tikkurila V484 | | | аналог по характеристикам | шт. | 1 | | пом. 13 |

| | | | | | | |
|---|---|---|---|---|---|---|
| | | | | | Проект: Четырёхкомнатная квартира | |
| | Лист | № док. | Подпись | Дата | | |
| Дизайнер | Кырлан А.С. | | | 04.11.26 | Спецификация мебели и оборудования (продолжение) | Стадия: П; Лист: 19; Листов: 120 |

| Поз. | Наименование и техническая характеристика | Тип, марка, обозначение документа, опросного листа | Код продукции | Поставщик | Ед. измерения | Кол. | Масса 1 ед., кг | Примечание |
|---|---|---|---|---|---|---|---|---|
| | **Декор** | | | | | | | |
| ДК1 | Картина над диваном: крупная абстракция, холст, тонкая рама; 1400×900 мм; низ на 1000 мм от пола | | | аналог по характеристикам | шт. | 1 | 6 | пом. 1; крепление: планка на дюбелях, 4 точки |
| ДК2 | Зеркало над буфетом, рама шпон дуба; 1000×800 мм; низ на 1100 мм от пола | | | аналог по характеристикам | шт. | 1 | 12 | пом. 1; крепление: анкер химический, 4 точки |
| ДК3 | Фикус лировидный в кашпо Ø400; 450×450 мм | | | аналог по характеристикам | шт. | 1 | | пом. 1 |
| ДК4 | Зеркало над раковиной C_03, влагостойкое; 600×800 мм; низ на 1100 мм от пола | | | аналог по характеристикам | шт. | 1 | 5 | пом. 2; крепление: зеркалодержатели, 4 точки |
| ДК5 | Картина над изголовьем: графика, паспарту, рама; 1100×700 мм; низ на 1300 мм от пола | | | аналог по характеристикам | шт. | 1 | 4 | пом. 4; крепление: две петли на дюбелях |
| ДК6 | Зеркало над комодом M_16; 700×900 мм; низ на 1050 мм от пола | | | аналог по характеристикам | шт. | 1 | 8 | пом. 4; крепление: анкер химический, 4 точки |
| ДК7 | Хлорофитум хохлатый в напольном кашпо Ø380; 420×420 мм | | | аналог по характеристикам | шт. | 1 | | пом. 4 |
| ДК8 | Часы настенные Ø400; 400×400 мм; центр на 1550 мм от пола | | | аналог по характеристикам | шт. | 1 | 2 | пом. 6; крепление: дюбель с крюком, 1 точка |
| ДК9 | Хлорофитум хохлатый на подоконнике (отм. +0,800); 300×200 мм; низ на 800 мм от пола | | | аналог по характеристикам | шт. | 1 | | пом. 6 |
| ДК10 | Зеркало над консолью M_30; 700×1000 мм; низ на 1050 мм от пола | | | аналог по характеристикам | шт. | 1 | 9 | пом. 7; крепление: анкер химический, 4 точки |
| ДК11 | Замиокулькас в напольном кашпо Ø360; 400×400 мм | | | аналог по характеристикам | шт. | 1 | | пом. 7 |
| ДК12 | Картина над изголовьем: графика, паспарту, рама; 600×800 мм; низ на 1200 мм от пола | | | аналог по характеристикам | шт. | 1 | 3 | пом. 9; крепление: две петли на дюбелях |
| ДК13 | Постер в раме, левый (группа «постеры»); 400×500 мм; низ на 1250 мм от пола | | | аналог по характеристикам | шт. | 1 | 2 | пом. 9; крепление: петля на дюбеле |
| ДК14 | Постер в раме, средний (группа «постеры»); 400×500 мм; низ на 1250 мм от пола | | | аналог по характеристикам | шт. | 1 | 2 | пом. 9; крепление: петля на дюбеле |
| ДК15 | Постер в раме, правый (группа «постеры»); 400×500 мм; низ на 1250 мм от пола | | | аналог по характеристикам | шт. | 1 | 2 | пом. 9; крепление: петля на дюбеле |
| ДК16 | Спатифиллум в напольном кашпо Ø360; 400×400 мм | | | аналог по характеристикам | шт. | 1 | | пом. 9 |
| ДК17 | Зеркало над раковиной C_07, влагостойкое; 500×700 мм; низ на 1150 мм от пола | | | аналог по характеристикам | шт. | 1 | 4 | пом. 10; крепление: зеркалодержатели, 4 точки |
| ДК20 | Картина: тёмная лиловая абстракция, холст, тонкая рама; 800×600 мм; низ на 1300 мм от пола | | | аналог по характеристикам | шт. | 1 | 4 | пом. 11; крепление: планка на дюбелях, 2 точки |
| ДК21 | Ваза напольная, керамика матовая; 300×300 мм | | | аналог по характеристикам | шт. | 1 | | пом. 11 |
| ДК18 | Зеркало ростовое 500×1600; 500×1600 мм; низ на 250 мм от пола | | | аналог по характеристикам | шт. | 1 | 12 | пом. 12; крепление: анкер химический, 4 точки + опора снизу |
| ДК19 | Лавр благородный в напольном кашпо Ø380; 400×400 мм | | | аналог по характеристикам | шт. | 1 | | пом. 13 |

| | | | | | | | |
|---|---|---|---|---|---|---|---|
| | | | | | Проект: Четырёхкомнатная квартира | | |
| | Лист | № док. | Подпись | Дата | Спецификация мебели и оборудования (продолжение) | Стадия | Лист | Листов |
| Дизайнер | Кырлан А.С. | | | 04.11.26 | | П | 20 | 120 |

## Ведомость изделий

| Марка | Наименование | Пом. | Ш×Г×В, мм | Корпус | Фасад | Кромка, мм | Кол. |
|---|---|---|---|---|---|---|---|
| M_07 | Система хранения | 2 | 600×350×700 | ЛДСП 16 | без фасадов | 0,4 / 2 | 1 |
| M_08 | Система хранения | 3 | 2180×400×2400 | ЛДСП 16 | без фасадов | 0,4 / 2 | 1 |
| M_09 | Система хранения | 3 | 960×400×2400 | ЛДСП 16 | без фасадов | 0,4 / 2 | 1 |
| M_15 | Шкаф распашной | 4 | 1800×600×2400 | ЛДСП 16 | МДФ 18 мм, эмаль матовая | 0,4 / 2 | 1 |
| M_17 | Система хранения | 4 | 2000×350×2100 | ЛДСП 16 | без фасадов | 0,4 / 2 | 1 |
| M_18 | Система хранения | 5 | 1800×250×2400 | ЛДСП 16 | МДФ 18 мм, эмаль матовая | 0,4 / 2 | 1 |
| M_28 | Шкаф-купе | 7 | 1600×600×2400 | ЛДСП 16 | ЛДСП 10 мм в алюминиевом профиле | 0,4 / 2 | 1 |
| M_31 | Система хранения | 8 | 950×300×2400 | ЛДСП 16 | без фасадов | 0,4 / 2 | 1 |
| M_32 | Система хранения | 8 | 1060×500×300 | ЛДСП 16 | без фасадов | 0,4 / 2 | 1 |
| M_34 | Шкаф распашной | 9 | 2000×600×2400 | ЛДСП 16 | МДФ 18 мм, эмаль матовая | 0,4 / 2 | 1 |
| M_38 | Система хранения | 12 | 1800×600×2400 | ЛДСП 16 | без фасадов | 0,4 / 2 | 1 |
| M_39 | Система хранения | 13 | 1250×400×2000 | ЛДСП 16 | без фасадов | 0,4 / 2 | 1 |
| M_40 | Система хранения | 13 | 1250×380×2000 | ЛДСП 16 | без фасадов | 0,4 / 2 | 1 |
| M_19 | Пенал: холодильник встр. | 6 | 600×600×2300 | ЛДСП 16 | МДФ 18 мм, эмаль матовая | 0,4 / 2 | 1 |
| M_20 | Модуль нижний: ящики | 6 | 600×600×900 | ЛДСП 16 | МДФ 18 мм, эмаль матовая | 0,4 / 2 | 1 |
| M_23 | Модуль навесной: полки | 6 | 600×350×720 | ЛДСП 16 | МДФ 18 мм, эмаль матовая | 0,4 / 2 | 1 |
| M_21 | Модуль нижний: духовой шкаф, варочная | 6 | 600×600×900 | ЛДСП 16 | МДФ 18 мм, эмаль матовая | 0,4 / 2 | 1 |
| M_24 | Модуль навесной: полки | 6 | 600×350×600 | ЛДСП 16 | МДФ 18 мм, эмаль матовая | 0,4 / 2 | 1 |
| M_22 | Модуль нижний: ящики | 6 | 600×600×900 | ЛДСП 16 | МДФ 18 мм, эмаль матовая | 0,4 / 2 | 1 |
| M_25 | Модуль навесной: полки | 6 | 600×350×720 | ЛДСП 16 | МДФ 18 мм, эмаль матовая | 0,4 / 2 | 1 |
| M_27 | Пенал: полки | 6 | 1000×600×2300 | ЛДСП 16 | МДФ 18 мм, эмаль матовая | 0,4 / 2 | 1 |
| M_26 | Остров (M_26.1, M_26.2, M_26.3) | 6 | 1800×800×900 | ЛДСП 16 | МДФ 18 мм, эмаль матовая | 0,4 / 2 | 1 |

## Ведомость встраиваемой техники

| Поз. | Прибор | Ниша, вырез, мм | Вентиляция | Питание | Схема |
|---|---|---|---|---|---|
| M_19 | Холодильник встраиваемый, ниша 1780 | ниша 1780 × 560 × 550 | решётка в цоколе, канал за корпусом, выход сверху | Р20: M_20, H=150 — в соседнем модуле, за ящиком | по модели |
| M_21 | Духовой шкаф встраиваемый, 60 см | ниша 560 × 600, глубина ≥ 550 | зазор за шкафом, вырез в задней стенке | ЭВ4: M_22, H=150 — в соседнем модуле, за ящиком | по модели |
| M_21 | Варочная панель индукционная, 60 см | вырез в столешнице 560 × 490 | | ЭВ3: M_20, H=150 — в соседнем модуле, за ящиком | по модели |
| M_24 | Вытяжка встраиваемая в навесной модуль, 60 см | низ ≥ 650 над панелью | воздуховод к вентканалу, короб до потолка | Р21: M_24, H=2200 — в навесном модуле | по модели |
| M_26.2 | Мойка врезная / подстольная с сифоном | вырез по шаблону, ориентир 760 × 480 | | смеситель — выводы ВК | по модели |

## Ведомость фурнитуры

| № | Фурнитура | Тип, размер | Изделия | Кол. |
|---|---|---|---|---|
| 1 | Полкодержатель с фиксацией | ø5 мм | M_07, M_08, M_09, M_15, M_17, M_18, M_28, M_31, M_34, M_38, M_39, M_40, M_19, M_23, M_24, M_25, M_27 | 328 |
| 2 | Анкер по основанию стены | по таблице крепежа | M_07, M_08, M_09, M_15, M_17, M_18, M_28, M_31, M_32, M_34, M_38, M_39, M_40, M_23, M_24, M_25 | 95 |
| 3 | Уголок крепления к стене от опрокидывания | стальной | M_07, M_08, M_09, M_15, M_17, M_18, M_28, M_31, M_32, M_34, M_38, M_39, M_40, M_19, M_27 | 30 |
| 4 | Штанга выдвижная торцевая | L по глубине | M_08, M_09, M_17, M_39, M_40 | 9 |
| 5 | Опора регулируемая с цоколем на клипсах | ход 20 мм | M_08, M_09, M_15, M_17, M_18, M_28, M_31, M_34, M_38, M_39, M_40 | 78 |
| 6 | Петля накладная 110° с доводчиком | чашка 35 мм | M_15, M_18, M_34, M_19, M_23, M_24, M_25, M_27, M_26 | 100 |
| 7 | Штанга овальная 30×15, L = 876 | + 2 держателя | M_15 | 1 |
| 8 | Система дверей купе: профиль, направляющие, ролики | на 2 двери | M_28 | 1 |
| 9 | Ручка-профиль вертикальная | в цвет профиля | M_28 | 2 |
| 10 | Штанга овальная 30×15, L = 776 | + 2 держателя | M_28 | 1 |
| 11 | Полка для обуви выдвижная наклонная | ширина 776 | M_28 | 3 |
| 12 | Штанга овальная 30×15, L = 976 | + 2 держателя | M_34 | 1 |
| 13 | Штанга овальная 30×15, L = 579 | + 2 держателя | M_38 | 3 |
| 14 | Ручка-профиль | латунь матовая | M_19, M_20, M_23, M_21, M_24, M_22, M_25, M_27, M_26 | 26 |
| 15 | Опора кухонная регулируемая 100–120 мм | + клипса цоколя | M_19, M_20, M_21, M_22, M_27, M_26 | 34 |
| 16 | Направляющие полного выдвижения с доводчиком NL 500 | пара | M_20, M_21, M_22, M_26 | 13 |
| 17 | Навес регулируемый для навесного шкафа | пара на секцию | M_23, M_24, M_25 | 3 |
| 18 | Шина монтажная | L = 540 | M_23, M_24, M_25 | 3 |
| 19 | Уголок крепления острова к полу | стальной, в цоколе | M_26 | 4 |


## Примечания

1. Модели техники выбирает заказчик до изготовления мебели; ниши, вырезы и вентиляция — по монтажной схеме выбранной модели (условие гарантии), её номер вносится в ведомость.
2. Количество фурнитуры — по чертежам изделий; запас крепежа 5 %. Аналоги — по характеристикам (доводчик, нагрузка, ход).
3. Цвет корпусов, фасадов и профилей — по колерной карте проекта. Кромка — скрытые / видимые торцы, мм.


| | | | | | |
|---|---|---|---|---|---|
| | | | | | Проект: Четырёхкомнатная квартира |
| | Лист | № док. | Подпись | Дата | |
| Дизайнер | Кырлан А.С. | | | 04.11.26 | Ведомости изделий, техники и фурнитуры |

| Стадия | Лист | Листов |
|---|---|---|
| П | 21 | 120 |


### Фрагмент 1. Ванная комната (пом. 2)

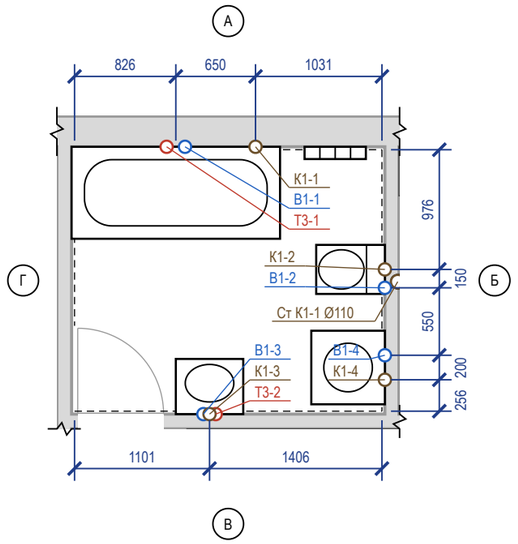


### Фрагмент 2. Кухня (пом. 6)

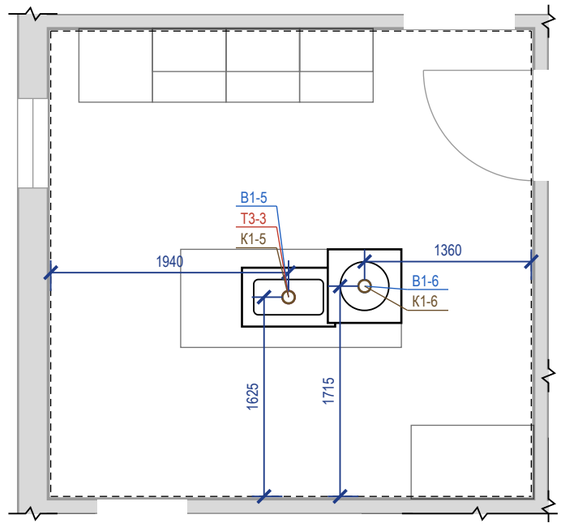


### Фрагмент 3. Санузел (пом. 10)

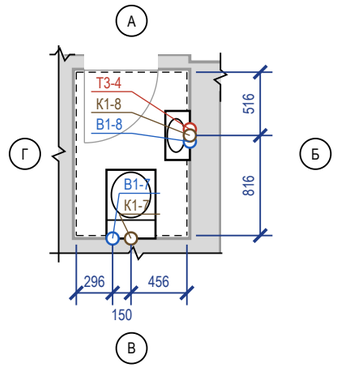


### Ведомость привязок выводов

| Код | Прибор | Ø | H, мм | Привязка от чист. стен, мм | Прим. |
|---|---|---|---|---|---|
| В1-1 | С_01 ванна | ½" | 800 | ст. А: 901 от Г | межос. 150 |
| Т3-1 | С_01 ванна | ½" | 800 | ст. А: 751 от Г | межос. 150 |
| К1-1 | С_01 ванна | Ø50 | 60 | ст. А: 1031 от Б | |
| В1-2 | С_02 унитаз подвесной | ½" | 250 | ст. Б: 1006 от В | в раме инсталляции |
| К1-2 | С_02 унитаз подвесной | Ø110 | 220 | ст. Б: 976 от А | |
| В1-3 | С_03 умывальник | ½" | 550 | ст. В: 1051 от Г | межос. 100 |
| Т3-2 | С_03 умывальник | ½" | 550 | ст. В: 1151 от Г | межос. 100 |
| К1-3 | С_03 умывальник | Ø40 | 450 | ст. В: 1101 от Г | |
| В1-4 | ОБ_02 стиральная машина | ½" | 700 | ст. Б: 456 от В | кран машины |
| К1-4 | ОБ_02 стиральная машина | Ø40 | 700 | ст. Б: 256 от В | |
| В1-5 | С_05 мойка кухонная | ½" | 600 | 1940 от Г; 1625 от В | межос. 100 |
| Т3-3 | С_05 мойка кухонная | ½" | 600 | 1940 от Г; 1625 от В | межос. 100 |
| К1-5 | С_05 мойка кухонная | Ø50 | 400 | 1940 от Г; 1625 от В | |
| В1-6 | ОБ_03 посудомоечная машина | ½" | 550 | 1360 от Б; 1715 от В | кран ПММ |
| К1-6 | ОБ_03 посудомоечная машина | Ø50 | 550 | 1360 от Б; 1715 от В | |
| В1-7 | С_06 унитаз подвесной | ½" | 250 | ст. В: 296 от Г | в раме инсталляции |
| К1-7 | С_06 унитаз подвесной | Ø110 | 220 | ст. В: 446 от Г | |
| В1-8 | С_07 умывальник | ½" | 550 | ст. Б: 566 от А | межос. 100 |
| Т3-4 | С_07 умывальник | ½" | 550 | ст. Б: 466 от А | межос. 100 |
| К1-8 | С_07 умывальник | Ø40 | 450 | ст. Б: 516 от А | |

### Условные обозначения


- вывод В1 (код — в ведомости привязок)
- вывод Т3 (код — в ведомости привязок)
- вывод К1 (код — в ведомости привязок)
- сантехприбор по расстановке (габарит модели)
- чистовая поверхность стены (от неё привязки)
- стояк «Ст К1-N / Ст В1-N» (ГОСТ 21.601), Ø мм
- стояк Т3 не на обмере — принят в шахте рядом со Ст В1, сверить
- линия обрыва (граница фрагмента)
- А — обозначение стены А–Г (как на развёртках)

### Примечания


1. Привязки выводов даны от чистовых поверхностей стен (облицовка на сторону: ванная комната — 24 мм (штукатурка 10 + клей 5 + плитка 9); кухня — 20 мм (по данным); санузел — 24 мм (штукатурка 10 + клей 5 + плитка 9)); эти же грани — на развёртках и в раскладке плитки. Высоты — от чистого пола помещения.
2. До черновой разводки сверить по паспорту выбранного прибора (смеситель, инсталляция, сифон).
3. Горячая вода (Т3) — слева от холодной (В1), если смотреть на прибор. Допуск установки выводов: ±5 мм в группе, ±20 мм у отдельно стоящих.
4. Расчёт систем водоснабжения и канализации и подбор оборудования выполняет проектная организация; лист задаёт места и высоты выводов.
5. С_05 мойка кухонная (В1-5, Т3-3, К1-5) — выводы в полу: пирог пола 170 мм их не укрывает (нужно 307 мм, расчёт — профиль К1 схемы разводки); до решения заказчика (подъём пола или другой смеситель / выпуск) не выполнять.
6. ОБ_03 посудомоечная машина (В1-6, К1-6) — выводы в полу: пирог пола 170 мм их не укрывает (нужно 257 мм, расчёт — профиль К1 схемы разводки); до решения заказчика (подъём пола или другой смеситель / выпуск) не выполнять.
7. Ст Т3-2 на обмере не показаны: приняты рядом с Ст В1-2 (в МКД стоят группой); положение сверить на объекте до разметки.
8. Стояки в коробах/шахтах не замоноличивать; стояк К1 в коробе — звукоизоляция стояка в коробе без жёсткого контакта с трубой; к арматуре и ревизиям — люк не меньше 300×400.
9. Штриховая линия чистовой грани стены прерывается на длине полотна открытой двери, лежащего вдоль грани (линии не должны сливаться при печати); положение грани — по размерам, а не по штриху.

| | | | | | | |
|---|---|---|---|---|---|---|
| | | | | | Проект: Четырёхкомнатная квартира | М 1:50 |
| | Лист | № док. | Подпись | Дата | План выводов сантехники | Стадия / Лист / Листов |
| Дизайнер | Кырлан А.С. | | | 04.11.26 | | П / 22 / 120 |


## План квартиры (М 1:400)

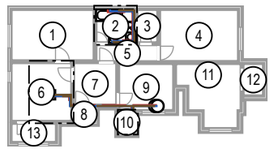



### Фр. 1. Ванная комната (М 1:40)

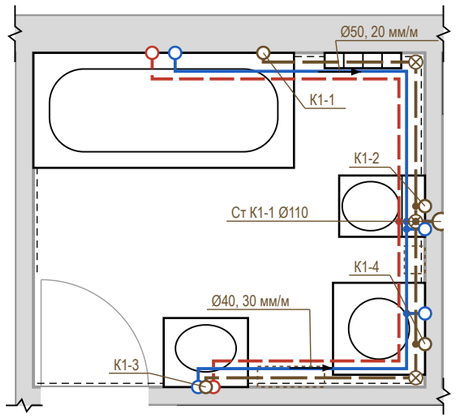


### Фр. 2. Кухня (М 1:40)

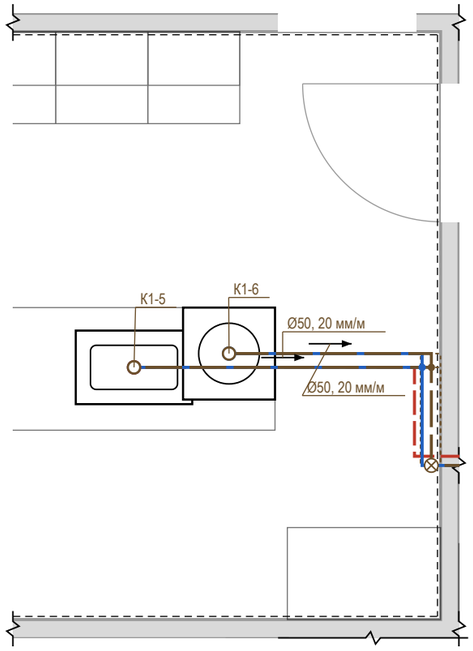


### Фр. 3. Санузел (М 1:40)

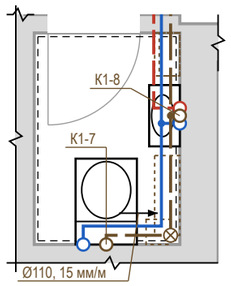


## Условные обозначения


- В1 — водопровод хозяйственно-питьевой (ХВС), PP-R Ø20
- Т3 — горячее водоснабжение, подача (ГВС), PP-R Ø20
- К1 — канализация бытовая
- направление уклона К1 / пола: Ø, мм на 1 м
- ⊗ ревизия (прочистка) К1 — доступ сохранить
- • тройник (ответвление к прибору)
- короб К1 над чистым полом (ГКЛВ под плитку)
- ○ вывод В1 (код — в ведомости привязок)
- ○ вывод Т3 (код — в ведомости привязок)
- ○ вывод К1 (код — в ведомости привязок)
- ▭ сантехприбор по расстановке (габарит модели)
- ○ стояк «Ст К1-N / Ст В1-N» (ГОСТ 21.601), Ø мм
- ◌ стояк Т3 не на обмере — принят в шахте рядом со Ст В1, сверить
- ⎍ линия обрыва (граница фрагмента)
- ▭ граница фрагмента на плане (Фр. N)

## Профиль выпусков К1 (до врезки в стояк)

| Выпуск | Прибор | Ø | L, м | i, мм/м | Δh, мм | Прокладка, мм |
|---|---|---|---|---|---|---|
| К1-7 | С_06 унитаз подвесной | Ø110 | 3,60 | 15 | 54 | короб 200×140 |
| К1-2 | С_02 унитаз подвесной | Ø110 | 0,35 | 20 | 7 | над полом за приборами |
| К1-5 | С_05 мойка кухонная | Ø50 | 10,10 | 20 | 202 | в полу не помещается: 307 > 170; до решения |
| К1-6 | ОБ_03 посудомоечная машина | Ø50 | 7,60 | 20 | 152 | в полу не помещается: 257 > 170; до решения |
| К1-1 | С_01 ванна | Ø50 | 2,30 | 20 | 46 | в полу, стяжка ≥ 151 |
| К1-3 | С_03 умывальник | Ø40 | 2,65 | 30 | 80 | короб 150×110 |
| К1-8 | С_07 умывальник | Ø40 | 2,50 | 30 | 75 | короб 150×110 |
| К1-4 | ОБ_02 стиральная машина | Ø40 | 1,05 | 30 | 32 | в полу, стяжка ≥ 127 |

Короб h×b: h — от чистого пола, b — от чистовой стены. Стяжка 155 мм — лист полов.

## Узел ввода В1, Т3 (схема, без масштаба)

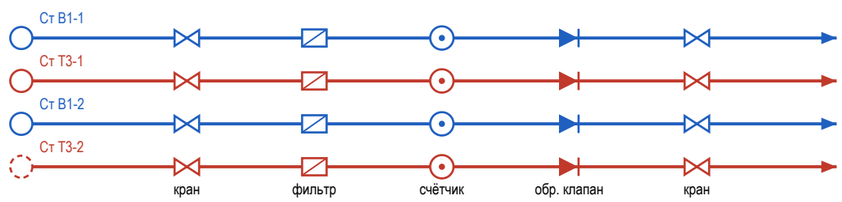


состав узла — по согласованию

⊗ Ст К1-1, Ст К1-2: ревизия на стояке — люк в коробе


## Примечания

1. Трассы принципиальные, построены от стояков вдоль стен помещений; фактическое положение фиксируется исполнительной схемой с привязками (фото с рулеткой) до закрытия.
2. Уклон К1 не менее 1/d и не более 150 мм/м (СП 30.13330.2020, п. 19.1), приняты практические уклоны; поворот — двумя отводами 45°, ревизия после поворота, доступ сохранить. Стояк К1 в коробе — звукоизоляция стояка в коробе, без жёсткого контакта короба с трубой.
3. Решение по К1: стяжка 155 мм не укрывает трубы (нужно Ø + Δh + 45 мм) — выпуски идут над чистым полом вдоль стен: К1-2 — за приборами и в раме инсталляции; К1-7, К1-3, К1-8 — в коробе ГКЛВ под плитку (размеры в профиле). Короба — на развёртках; отметку низа врезки в стояк замерить до черновых работ.
4. К1-5 (С_05 мойка кухонная, выпуск в пол): Δh 202 + Ø50 + 45 = 307 мм > пирога 170 мм — в стяжке не помещается, в короб не уходит: подиум или подъём пола на 140 мм или прибор ближе к стояку — решение заказчика; до решения не выполнять.
5. К1-6 (ОБ_03 посудомоечная машина, выпуск в пол): Δh 152 + Ø50 + 45 = 257 мм > пирога 170 мм — в стяжке не помещается, в короб не уходит: подиум или подъём пола на 90 мм или прибор ближе к стояку — решение заказчика; до решения не выполнять.
6. Состав узла ввода В1, Т3 — по согласованию: на схеме типовой узел — кран шаровой, фильтр, счётчик, обратный клапан, кран; состав и места не определены (записи реестра нет). Доступ к арматуре — через люк не меньше 300×400. Водопровод — в штробе стен или в коробах; трубы испытать давлением до закрытия (акт скрытых работ).
7. Расчёт систем, диаметры магистралей и подбор оборудования выполняет проектная организация; врезка и перенос стояков — по согласованию с управляющей организацией. Арматуру и привязки сверить по паспортам приборов.
8. Ст Т3-2 на обмере не показаны: приняты рядом с Ст В1-2 (в МКД стоят группой); положение сверить на объекте до разводки.
9. Штриховая линия чистовой грани стены прерывается на длине полотна открытой двери, лежащего вдоль грани (линии не должны сливаться при печати); положение грани — по размерам, а не по штриху.

| | | | | | |
|---|---|---|---|---|---|
| | | | | | Проект: Четырёхкомнатная квартира |
| | Лист | № док. | Подпись | Дата | Схема разводки водопровода и канализации |
| Дизайнер | Кырлан А.С. | | | 04.11.26 | |

| Стадия | Лист | Листов |
|---|---|---|
| П | 23 | 120 |

## Схема В1 (М 1:50; по вертикали и горизонтали один масштаб, глубина — ×0,5 под 45°)

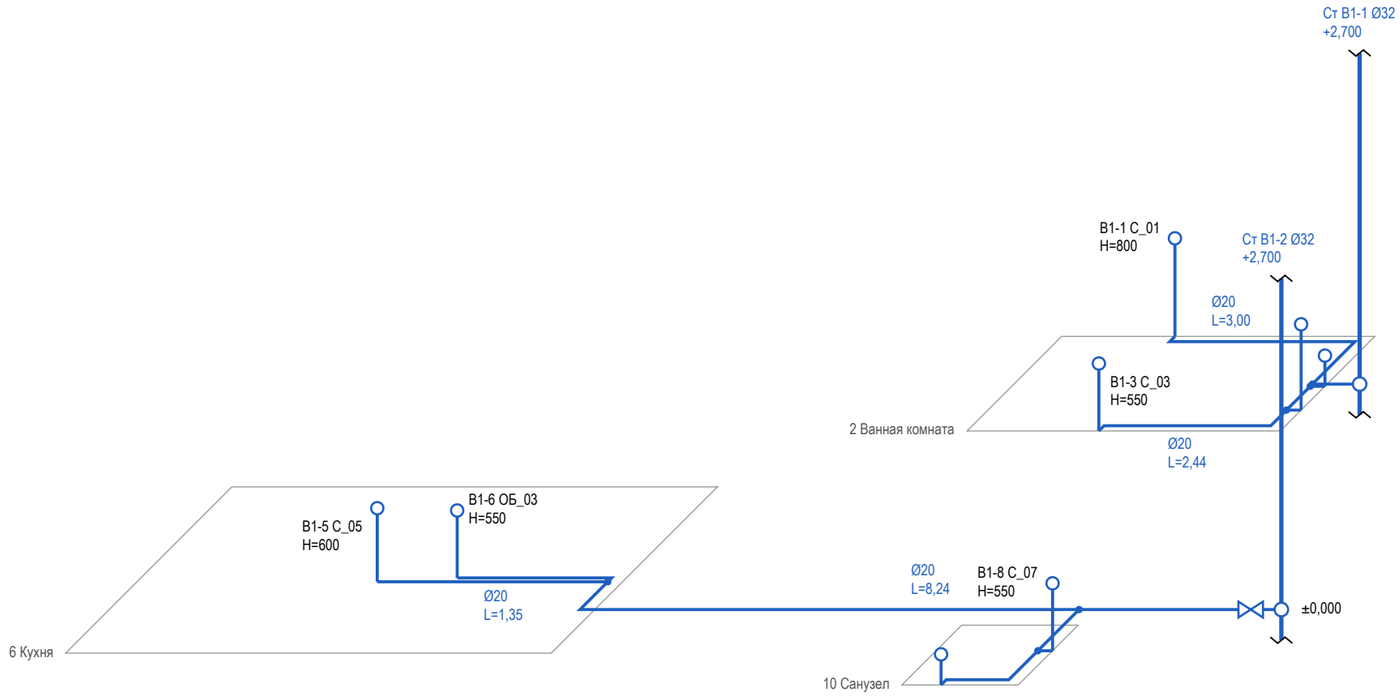


### Условные обозначения


- В1 — водопровод хозяйственно-питьевой (ХВС), PP-R Ø20
- вывод В1 (код — в ведомости привязок)
- стояк «Ст К1-N / Ст В1-N» (ГОСТ 21.601), Ø мм
- стояк в плане (на отметке пола); вертикаль — стояк по высоте, разрыв — перекрытие
- тройник (ответвление к прибору)
- кран шаровой

### Примечания

1. Схема В1 построена по тем же трассам, что план разводки: положение в плане сохранено, глубина — в масштабе ×0,5. Трассы принципиальные; фактическое положение фиксируется исполнительной схемой до закрытия.
2. Высоты H — от чистого пола помещения, мм. Отметка прокладки магистрали В1 (в стяжке, в стене или по полу) в данных не задана: участки показаны на уровне пола условно (записи реестра нет).
3. Узел ввода В1 (кран, фильтр, счётчик, обратный клапан, кран) — на схеме разводки; состав узла ввода — по согласованию. Кран шаровой — на первом участке от стояка.
4. Трубы испытать давлением до закрытия (акт скрытых работ, опрессовка по СП 73.13330.2016).
5. Диаметры, высоты выводов и места кранов — по паспортам выбранных приборов и расчёту проектной организации.
6. Расчёт систем, диаметры магистралей и подбор оборудования выполняет проектная организация.

| | | | | | | | |
|---|---|---|---|---|---|---|---|
| | | | | | Проект: Четырёхкомнатная квартира | | M 1:50 |
| | Лист | № док. | Подпись | Дата | Аксонометрическая схема В1 (холодное водоснабжение) | Стадия | Лист | Листов |
| Дизайнер | Кырлан А.С. | | | 04.11.26 | | П | 24 | 120 |

## Схема Т3 (М 1:50; по вертикали и горизонтали один масштаб, глубина — ×0,5 под 45°)

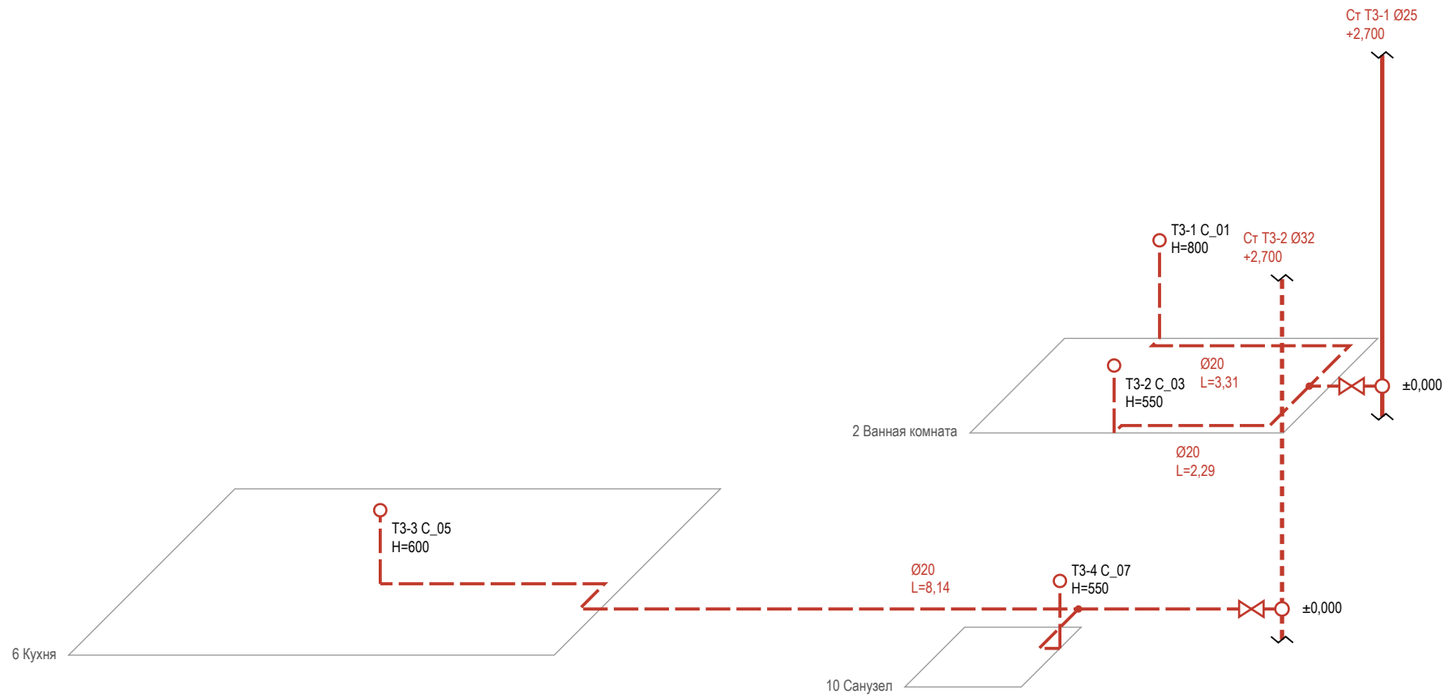


### Условные обозначения


- Т3 — горячее водоснабжение, подача (ГВС), PP-R Ø20
- вывод Т3 (код — в ведомости привязок)
- стояк «Ст К1-N / Ст В1-N» (ГОСТ 21.601), Ø мм
- стояк в плане (на отметке пола); вертикаль — стояк по высоте, разрыв — перекрытие
- тройник (ответвление к прибору)
- кран шаровой
- стояк Т3 не на обмере — принят в шахте рядом со Ст В1, сверить

### Примечания

1. Схема Т3 построена по тем же трассам, что план разводки: положение в плане сохранено, глубина — в масштабе ×0,5. Трассы принципиальные; фактическое положение фиксируется исполнительной схемой до закрытия.
2. Высоты Н — от чистого пола помещения, мм. Отметка прокладки магистрали Т3 (в стяжке, в стене или по полу) в данных не задана: участки показаны на уровне пола условно (записи реестра нет).
3. Узел ввода Т3 (кран, фильтр, счётчик, обратный клапан, кран) — на схеме разводки; состав узла ввода — по согласованию. Кран шаровой — на первом участке от стояка.
4. Циркуляция ГВС в данных не задана — циркуляционного трубопровода на схеме нет (записи реестра нет).
5. Ст Т3-2 на обмере не показаны: приняты рядом с Ст В1-2 (в МКД стоят группой); положение сверить на объекте до разводки.
6. Трубы испытать давлением до закрытия (акт скрытых работ, опрессовка по СП 73.13330.2016).
7. Диаметры, высоты выводов и места кранов — по паспортам выбранных приборов и расчёту проектной организации.
8. Расчёт систем, диаметры магистралей и подбор оборудования выполняет проектная организация.

| | | | | | | | |
|---|---|---|---|---|---|---|---|
| | | | | | Проект: Четырёхкомнатная квартира | | M 1:50 |
| | Лист | № док. | Подпись | Дата | Аксонометрическая схема Т3 (горячее водоснабжение) | Стадия | Лист | Листов |
| Дизайнер | Кырлан А.С. | | | 04.11.26 | | П | 25 | 120 |

## Схема К1 (М 1:50; по вертикали и горизонтали один масштаб, глубина — ×0,5 под 45°)

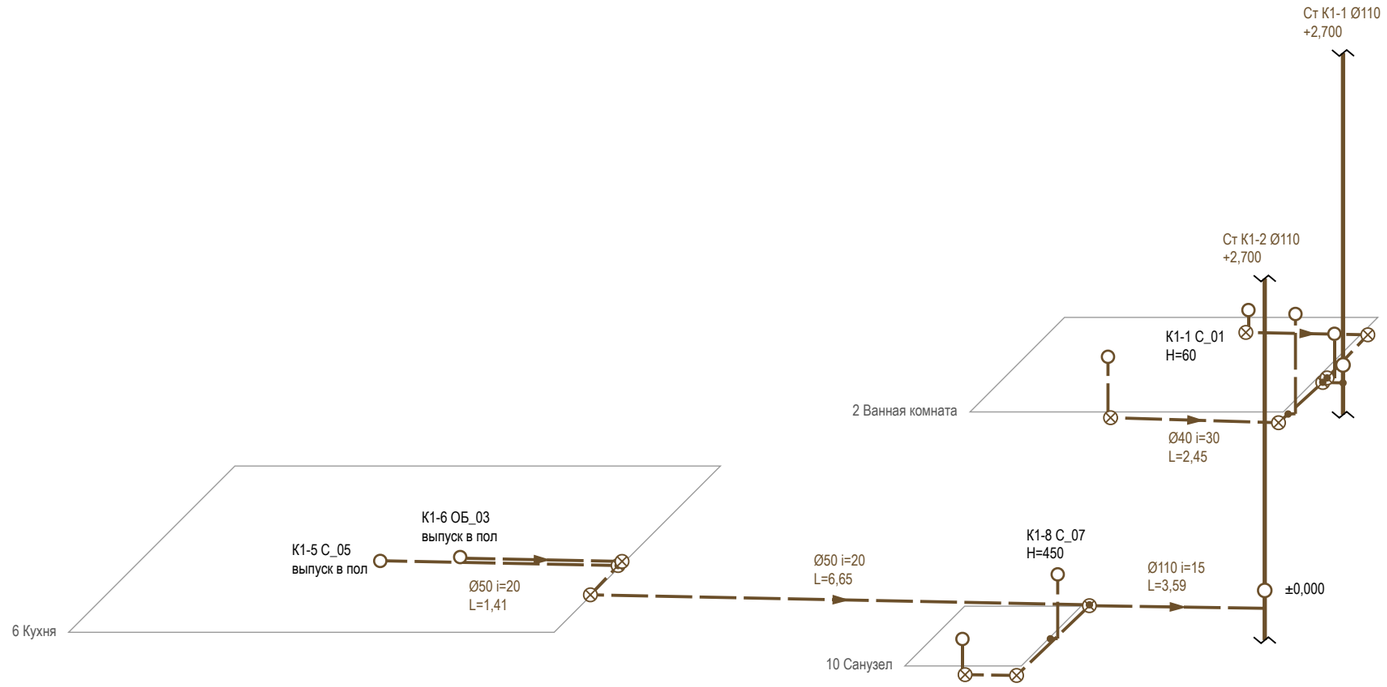


### Условные обозначения


- К1 — канализация бытовая
- вывод К1 (код — в ведомости привязок)
- стояк «Ст К1-N / Ст В1-N» (ГОСТ 21.601), Ø мм
- стояк в плане (на отметке пола); вертикаль — стояк по высоте, разрыв — перекрытие
- направление уклона К1 / пола: Ø, мм на 1 м
- ревизия (прочистка) К1 — доступ сохранить
- тройник (ответвление к прибору)

### Примечания


1. Схема К1 построена по тем же трассам, что план разводки: положение в плане сохранено, глубина — в масштабе ×0,5. Трассы принципиальные; фактическое положение фиксируется исполнительной схемой до закрытия.
2. Отметки — от плиты перекрытия: низ трубы у врезки в стояк — отметка из данных выпуска, к прибору труба поднимается на уклон i, мм/м (уклон не менее 1/d и не более 150 мм/м, СП 30.13330.2020, п. 19.1); чистый пол — выше плиты на стяжку (высота пирога пола). Высота выпуска прибора H — от чистого пола.
3. Ревизия — на повороте и в начале участка; стояк К1 в коробе с люком — звукоизоляция стояка в коробе; поворот — двумя отводами 45°.
4. Трубы испытать давлением до закрытия (акт скрытых работ, опрессовка по СП 73.13330.2016).
5. Диаметры, высоты выводов и места кранов — по паспортам выбранных приборов и расчёту проектной организации.
6. Расчёт систем, диаметры магистралей и подбор оборудования выполняет проектная организация.

| | | | | | | | |
|---|---|---|---|---|---|---|---|
| | | | | | Проект: Четырёхкомнатная квартира | | М 1:50 |
| | Лист | № док. | Подпись | Дата | Аксонометрическая схема К1 (канализация) | Стадия | Лист | Листов |
| Дизайнер | Кырлан А.С. | | | 04.11.26 | | П | 26 | 120 |

## Стена А (М 1:20)

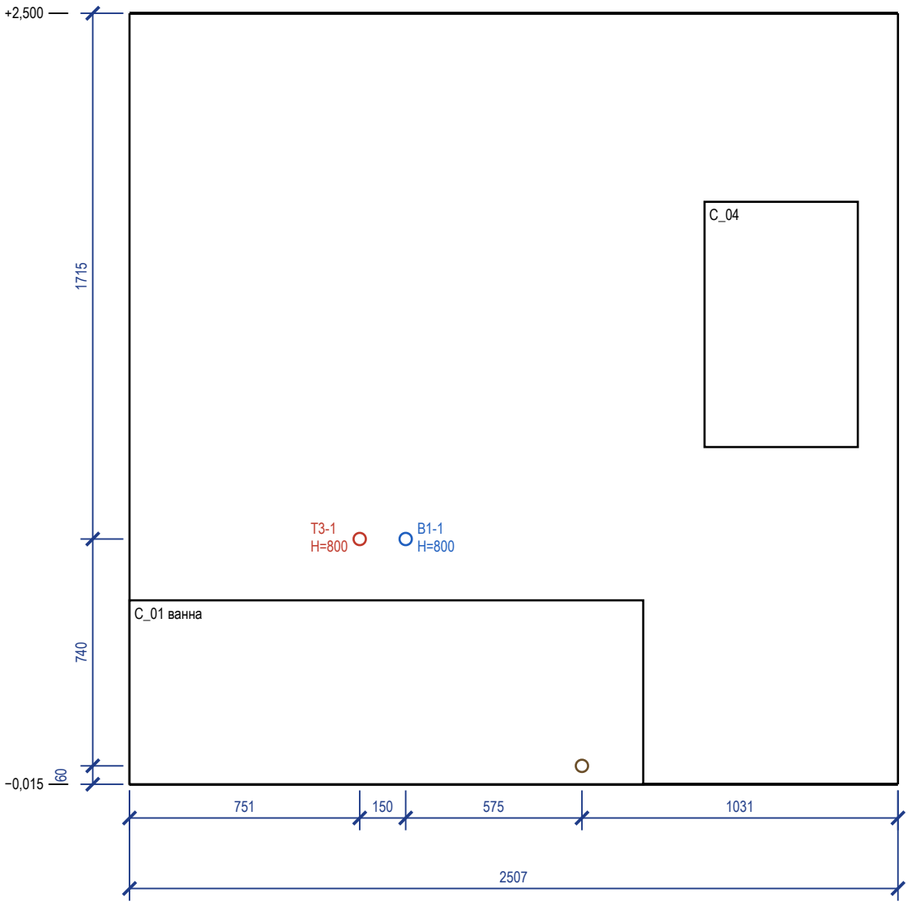


## Стена Б (М 1:20)

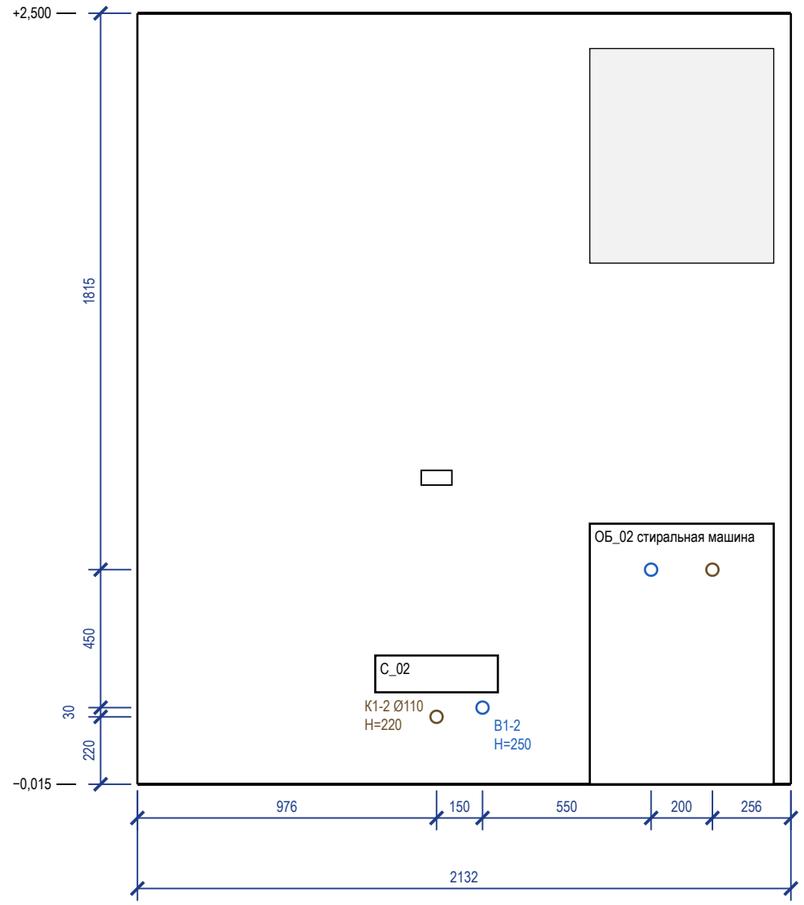


## Ведомость привязок выводов (от чистого пола и угла)

| Код | Прибор | Ø | H, мм | Привязка, мм |
|---|---|---|---|---|
| B1-1 | C_01 ванна | ½" | 800 | ст. А: 901 от лев. угла |
| T3-1 | C_01 ванна | ½" | 800 | ст. А: 751 от лев. угла |
| K1-1 | C_01 ванна | Ø50 | 60 | ст. А: 1476 от лев. угла |
| B1-2 | C_02 унитаз подвесной | ½" | 250 | ст. Б: 1126 от лев. угла |
| K1-2 | C_02 унитаз подвесной | Ø110 | 220 | ст. Б: 976 от лев. угла |
| B1-4 | ОБ_02 стиральная машина | ½" | 700 | ст. Б: 1676 от лев. угла |
| K1-4 | ОБ_02 стиральная машина | Ø40 | 700 | ст. Б: 1876 от лев. угла |

## Условные обозначения


- вывод B1 (код — в ведомости привязок)
- вывод T3 (код — в ведомости привязок)
- вывод K1 (код — в ведомости привязок)
- сантехприбор по расстановке (габарит модели)
- дверной проём; окно — сплошной контур
- кнопка смыва инсталляции (H — по данным прибора)

## Примечания


1. Габариты и высоты приборов, межосевые смесителей и места кранов — по паспортам выбранных приборов, сверяются до разметки стен.
2. Высоты H — от чистого пола помещения, мм; отметка чистого пола и потолка — у левого края вида (от ±0,000 объекта). Привязки — от левого чистового угла вида (облицовка стен вычтена), как на развёртках стен.
3. Кнопка смыва C_02 — H=1000 (по данным прибора).
4. Ревизионные люки (ревизия K1 в коробе за стиральной машиной 300×400): место в стене на развёртке не задано (записи реестра нет).
5. Часть подписей выводов не уместилась у знака: коды и высоты — в ведомости привязок.
6. Помещение «Ванная комната» — 2 листа: стены 1) А, Б; 2) В, Г.
7. Расчёт систем водоснабжения и канализации и подбор оборудования выполняет проектная организация; лист задаёт места и высоты выводов.

| | | | | | | |
|---|---|---|---|---|---|---|
| | | | | | Проект: Четырёхкомнатная квартира | М 1:20 |
| | Лист | № док. | Подпись | Дата | | |
| Дизайнер | Кырлан А.С. | | | 04.11.26 | Развёртки мокрых зон: выводы ВК. Ванная комната (лист 1 из 2) | Стадия: П; Лист: 27; Листов: 120 |

## Стена В (М 1:20)

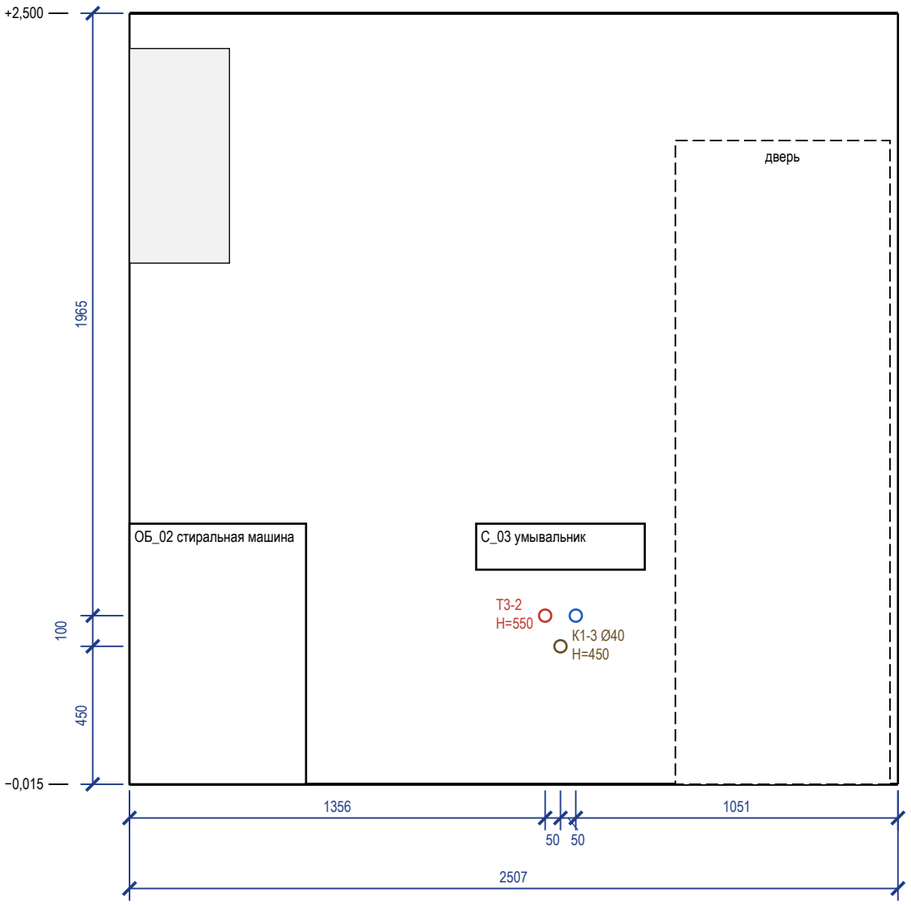


## Стена Г (М 1:20)

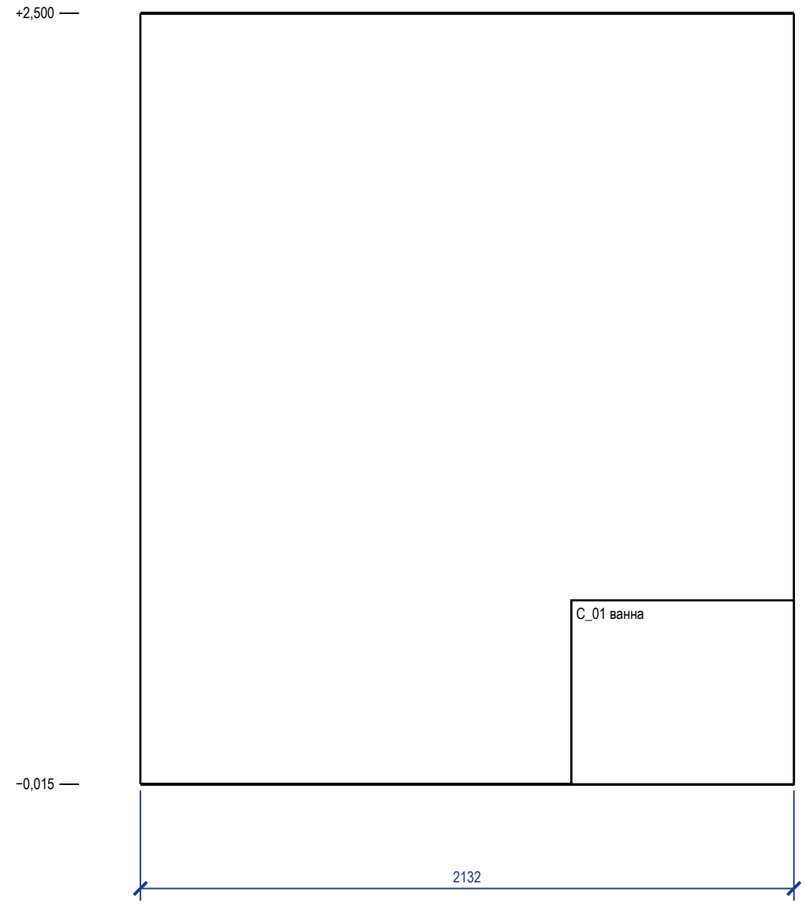


## Ведомость привязок выводов (от чистого пола и угла)

| Код | Прибор | Ø | H, мм | Привязка, мм |
|---|---|---|---|---|
| В1-3 | С_03 умывальник | ½" | 550 | ст. В: 1456 от лев. угла |
| Т3-2 | С_03 умывальник | ½" | 550 | ст. В: 1356 от лев. угла |
| К1-3 | С_03 умывальник | Ø40 | 450 | ст. В: 1406 от лев. угла |

## Условные обозначения

- вывод В1 (код — в ведомости привязок)
- вывод Т3 (код — в ведомости привязок)
- вывод К1 (код — в ведомости привязок)
- сантехприбор по расстановке (габарит модели)
- дверной проём; окно — сплошной контур

## Примечания

1. Габариты и высоты приборов, межосевые смесителей и места кранов — по паспортам выбранных приборов, сверяются до разметки стен.
2. Высоты H — от чистого пола помещения, мм; отметка чистого пола и потолка — у левого края вида (от ±0,000 объекта). Привязки — от левого чистового угла вида (облицовка стен вычтена), как на развёртках стен.
3. Ревизионные люки (ревизия К1 в коробе за стиральной машиной 300×400): место в стене на развёртке не задано (записи реестра нет).
4. Часть подписей выводов не уместилась у знака: коды и высоты — в ведомости привязок.
5. Помещение «Ванная комната» — 2 листа: стены 1) А, Б; 2) В, Г.
6. Расчёт систем водоснабжения и канализации и подбор оборудования выполняет проектная организация; лист задаёт места и высоты выводов.

| | | | | | |
|---|---|---|---|---|---|
| | | | | | Проект: Четырёхкомнатная квартира — М 1:20 |
| | Лист | № док. | Подпись | Дата | |
| Дизайнер | Кырлан А.С. | | | 04.11.26 | Развёртки мокрых зон: выводы ВК. Ванная комната (лист 2 из 2) |

| Стадия | Лист | Листов |
|---|---|---|
| П | 28 | 120 |

## Ведомость привязок выводов (от чистого пола и угла)

| Код | Прибор | Ø | H, мм | Привязка, мм |
|---|---|---|---|---|
| **Стен с приборами нет.** Развёртка не построена: выводы В1, Т3, К1 не назначены, привязки не даются; расстановка приборов в данных не задана (записи реестра нет). | | | | |
| | выводов на стене нет | | | |

## Условные обозначения


- вывод В1 (код — в ведомости привязок)
- вывод Т3 (код — в ведомости привязок)
- вывод К1 (код — в ведомости привязок)
- сантехприбор по расстановке (габарит модели)
- дверной проём; окно — сплошной контур

## Примечания


1. Габариты и высоты приборов, межосевые смесителей и места кранов — по паспортам выбранных приборов, сверяются до разметки стен.
2. Высоты H — от чистого пола помещения, мм; отметка чистого пола и потолка — у левого края вида (от ±0,000 объекта). Привязки — от левого чистового угла вида (облицовка стен вычтена), как на развёртках стен.
3. Приборы С_05, ОБ_03: стена не определена, на развёртке не показаны (записи реестра нет).
4. Выводы в полу (К1-1, К1-2): трап, лоток, выпуск отдельностоящей ванны, подвод к стойке напольного смесителя — на развёртке их нет; место и пирог пола — лист «Схема разводки» (профиль К1, узел 1).
5. Ревизионные люки к арматуре и ревизиям в данных не заданы: место и размер не определены (записи реестра нет).
6. Мойка, ПММ и фильтр — выводы в шкафу мойки; диаметры и положение сифона и кранов сверить по паспортам приборов и чертежам модуля.
7. Расчёт систем водоснабжения и канализации и подбор оборудования выполняет проектная организация; лист задаёт места и высоты выводов.

| | | | | | | |
|---|---|---|---|---|---|---|
| | | | | | Проект: Четырёхкомнатная квартира | **М 1:20** |
| | Лист | № док. | Подпись | Дата | | |
| Дизайнер | Кырлан А.С. | | | 04.11.26 | Развёртки мокрых зон: выводы ВК. Кухня | Стадия: П; Лист: 29; Листов: 120 |

### Стена Б (М 1:20)

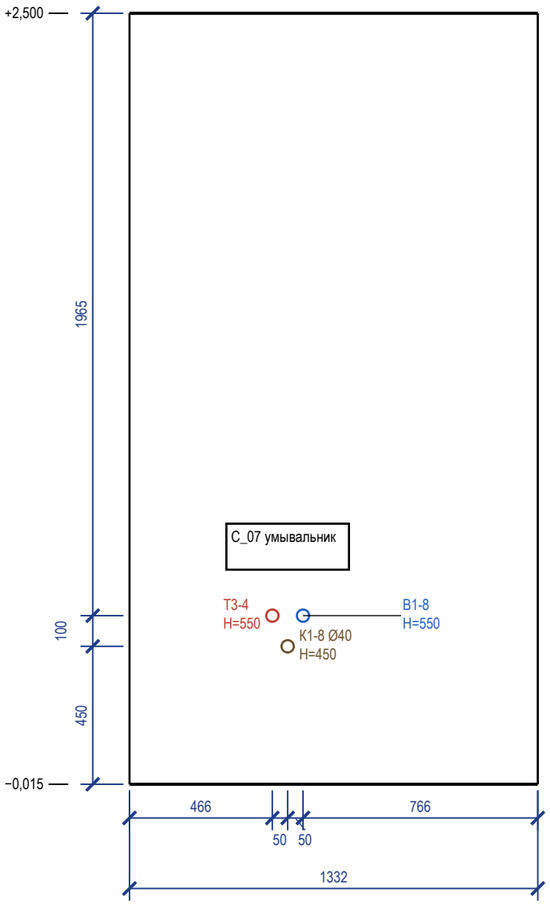


### Стена В (М 1:20)

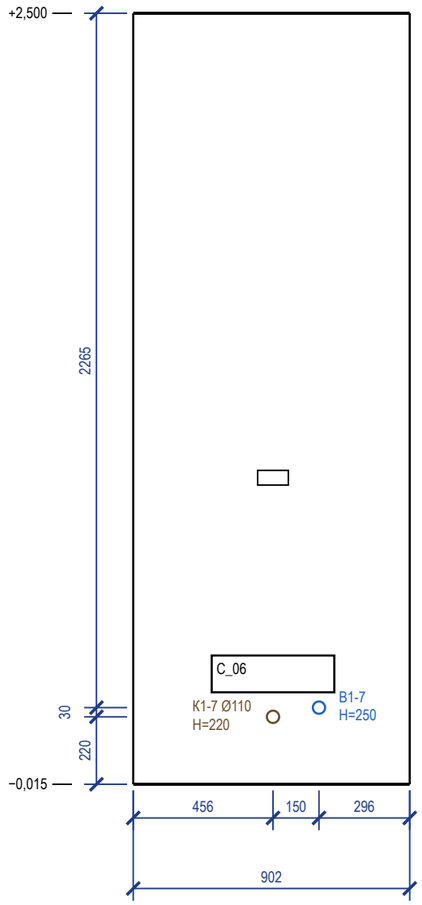


### Ведомость привязок выводов (от чистого пола и угла)

| Код | Прибор | Ø | H, мм | Привязка, мм |
|---|---|---|---|---|
| B1-8 | C_07 умывальник | ½" | 550 | ст. Б: 566 от лев. угла |
| T3-4 | C_07 умывальник | ½" | 550 | ст. Б: 466 от лев. угла |
| K1-8 | C_07 умывальник | Ø40 | 450 | ст. Б: 516 от лев. угла |
| B1-7 | C_06 унитаз подвесной | ½" | 250 | ст. В: 606 от лев. угла |
| K1-7 | C_06 унитаз подвесной | Ø110 | 220 | ст. В: 456 от лев. угла |

### Условные обозначения

- вывод B1 (код — в ведомости привязок)
- вывод T3 (код — в ведомости привязок)
- вывод K1 (код — в ведомости привязок)
- сантехприбор по расстановке (габарит модели)
- дверной проём; окно — сплошной контур
- кнопка смыва инсталляции (H — по данным прибора)

### Примечания

1. Габариты и высоты приборов, межосевые смесителей и места кранов — по паспортам выбранных приборов, сверяются до разметки стен.
2. Высоты H — от чистого пола помещения, мм; отметка чистого пола и потолка — у левого края вида (от ±0,000 объекта). Привязки — от левого чистового угла вида (облицовка стен вычтена), как на развёртках стен.
3. Кнопка смыва C_06 — H=1000 (по данным прибора).
4. Ревизионные люки к арматуре и ревизиям в данных не заданы: место и размер не определены (записи реестра нет).
5. Расчёт систем водоснабжения и канализации и подбор оборудования выполняет проектная организация; лист задаёт места и высоты выводов.

| | | | | | | |
|---|---|---|---|---|---|---|
| | | | | | Проект: Четырёхкомнатная квартира | М 1:20 |
| | | | | | | |
| | Лист | № док. | Подпись | Дата | | |
| Дизайнер | Кырлан А.С. | | | 04.11.26 | Развёртки мокрых зон: выводы ВК. Санузел | |
| | | | | | | |


| Стадия | Лист | Листов |
|---|---|---|
| П | 30 | 120 |

| Поз. | Наименование и техническая характеристика | Тип, марка, обозначение документа | Код продукции | Поставщик | Ед. изм. | Кол. | Масса 1 ед., кг | Примечание |
|---|---|---|---|---|---|---|---|---|
| | Санитарные приборы | | | | | | | |
| 1 | Ванна встраиваемая акриловая 1700×750 мм, с каркасом, экраном и отверстием слив-перелив | аналог | | выбор заказчика | шт | 1 | 35 | С_01 |
| 2 | Унитаз подвесной безободковый, с сиденьем микролифт, крепёж и звукоизолирующая прокладка | аналог | | выбор заказчика | шт | 2 | | С_02, С_06 |
| 3 | Инсталляция для подвесного унитаза: рама высотой 1120 мм, бачок, клавиша смыва (ось клавиши 1050 мм от чистого пола) | аналог | | выбор заказчика | шт | 2 | | С_02, С_06; короб ГКЛВ |
| 4 | Умывальник подвесной 550×450 мм, с отверстием под смеситель и переливом | аналог | | выбор заказчика | шт | 1 | | С_03 |
| 5 | Умывальник подвесной 400×200 мм, с отверстием под смеситель и переливом | аналог | | выбор заказчика | шт | 1 | | С_07 |
| 6 | Мойка кухонная врезная 760×480 мм, с переливом | аналог | | с кухонной мебелью | шт | 1 | | С_05 |
| 7 | Полотенцесушитель электрический, IP44, с терморегулятором | аналог | | выбор заказчика | шт | 1 | | С_04 |
| | Смесители, сифоны и арматура приборов | | | | | | | |
| 8 | Смеситель для ванны настенный однорычажный, межосевое 150 мм, с душевым набором (лейка, шланг, держатель) | аналог | | выбор заказчика | шт | 1 | | С_01 |
| 9 | Смеситель для умывальника однорычажный, с донным клапаном | аналог | | выбор заказчика | шт | 2 | | С_03, С_07 |
| 10 | Смеситель кухонный однорычажный, высокий излив | аналог | | выбор заказчика | шт | 1 | | С_05 |
| 11 | Обвязка ванны слив-перелив Ø40/50 с сифоном | аналог | | выбор заказчика | шт | 1 | | С_01 |
| 12 | Сифон для умывальника бутылочный Ø32/40–50, с гофрой к выпуску | аналог | | выбор заказчика | шт | 2 | | С_03, С_07 |
| 13 | Сифон для мойки Ø40/50 | аналог | | выбор заказчика | шт | 1 | | С_05 |
| 14 | Сифон для посудомоечной машины с обратным клапаном, на выводе слива Ø40 | аналог | | выбор заказчика | шт | 1 | | ОБ_03 |
| 15 | Сифон для стиральной машины встраиваемый в стену Ø50, с обратным клапаном | аналог | | выбор заказчика | шт | 1 | | ОБ_02 |
| 16 | Кран угловой ½"×½" с гибкой подводкой 40 см (умывальники, мойка) | аналог | | выбор заказчика | шт | 6 | | по 2 на прибор |
| 17 | Кран шаровой угловой ½"×¾" для подключения стиральной и посудомоечной машины | аналог | | выбор заказчика | шт | 2 | | ОБ_02, ОБ_03 |
| | Трубопроводы | | | | | | | |
| 18 | Труба полипропиленовая PP-R PN20 Ø20×3,4 (В1) | ГОСТ 32415-2013 | | выбор заказчика | м | 24,5 | 0,17 | 17,6 + 4,3 + 10 % |
| 19 | Труба PP-R, армированная стекловолокном, PN20 Ø20×2,8 (Т3) | ГОСТ 32415-2013 | | выбор заказчика | м | 19,5 | 0,15 | 14,8 + 2,5 + 10 % |
| 20 | Труба канализационная ПП Ø40 (К1) | ГОСТ 32414-2013 | | выбор заказчика | м | 5 | | 2,6 + 1,6 + 10 % |
| 21 | Труба канализационная ПП Ø50 (К1) | ГОСТ 32414-2013 | | выбор заказчика | м | 12,5 | | 10,1 + 1,0 + 10 % |
| 22 | Труба канализационная ПП Ø110 (К1) | ГОСТ 32414-2013 | | выбор заказчика | м | 5 | | 3,9 + 0,4 + 10 % |
| | Фасонные части и выводы | | | | | | | |
| 23 | Отвод канализационный ПП 45° Ø40 | ГОСТ 32414-2013 | | выбор заказчика | шт | 4 | | 2 шт. на поворот |
| 24 | Отвод канализационный ПП 45° Ø50 | ГОСТ 32414-2013 | | выбор заказчика | шт | 10 | | 2 шт. на поворот |
| 25 | Отвод канализационный ПП 45° Ø110 | ГОСТ 32414-2013 | | выбор заказчика | шт | 10 | | 2 шт. на поворот |
| 26 | Тройник канализационный ПП 45° (врезки ветвей) | ГОСТ 32414-2013 | | выбор заказчика | шт | 7 | | |
| 27 | Ревизия канализационная ПП (после поворота трассы) | ГОСТ 32414-2013 | | выбор заказчика | шт | 6 | | доступ сохранить |
| 28 | Фитинги PP-R Ø20: тройники, угольники 90° (ветви и повороты В1, Т3) | ГОСТ 32415-2013 | | выбор заказчика | шт | 28 | | |
| 29 | Водорозетка PP-R Ø20×½" настенная, с креплением | ГОСТ 32415-2013 | | выбор заказчика | шт | 12 | | коды — лист выводов |
| | Узлы ввода, люки, короба | | | | | | | |
| 30 | Кран шаровой латунный Ду15 PN16 (отключение ввода) | аналог | | выбор заказчика | шт | 4 | | Ст В1-1, Ст Т3-1, Ст В1-2, Ст Т3-2 |
| 31 | Фильтр сетчатый косой Ду15 | аналог | | выбор заказчика | шт | 4 | | |
| 32 | Счётчик воды крыльчатый Ду15 (ХВ, ГВ), с поверкой | аналог | | выбор заказчика | шт | 4 | | пломба УК |
| 33 | Клапан обратный Ду15 | аналог | | выбор заказчика | шт | 4 | | |
| 34 | Люк ревизионный нажимной под плитку 300×400 мм | аналог | | выбор заказчика | шт | 4 | | к стоякам и арматуре |
| 35 | Звукоизоляция стояка К1 в коробе: рулонный звукоизоляционный материал ≥ 10 мм, обмотка стояка на высоту этажа | аналог | | выбор заказчика | м | 5,4 | | Ст К1-1, Ст К1-2 |
| 36 | Короб К1 над полом: профиль ПН/ПС, ГКЛВ 12,5 мм под плитку | аналог | | выбор заказчика | м | 5,8 | | сечение — лист разводки |

## Примечания

1. Форма 1 ГОСТ 21.110-2013, ширины граф изменены по п. 4.1. «Аналог» — аналог по характеристикам: модели внести до черновых работ, привязки выводов сверить по паспортам.
2. Бытовая техника не входит (показана арматура подключения), мойка — в комплекте кухни (марка — модуля кухни, как у столяра). Длины труб — трасса листа разводки + подъёмы + 10 %.
3. Стояк К1 в коробе — звукоизоляция стояка в коробе без жёсткого контакта короба с трубой.
4. Расчёт систем водоснабжения и канализации, диаметры магистралей и подбор оборудования выполняет проектная организация.

| | | | | | Проект: Четырёхкомнатная квартира | | | |
|---|---|---|---|---|---|---|---|---|
| | Лист | № док. | Подпись | Дата | Спецификация сантехнического оборудования | Стадия | Лист | Листов |
| Дизайнер | Кырлан А.С. | | | 04.11.26 | | П | 31 | 120 |

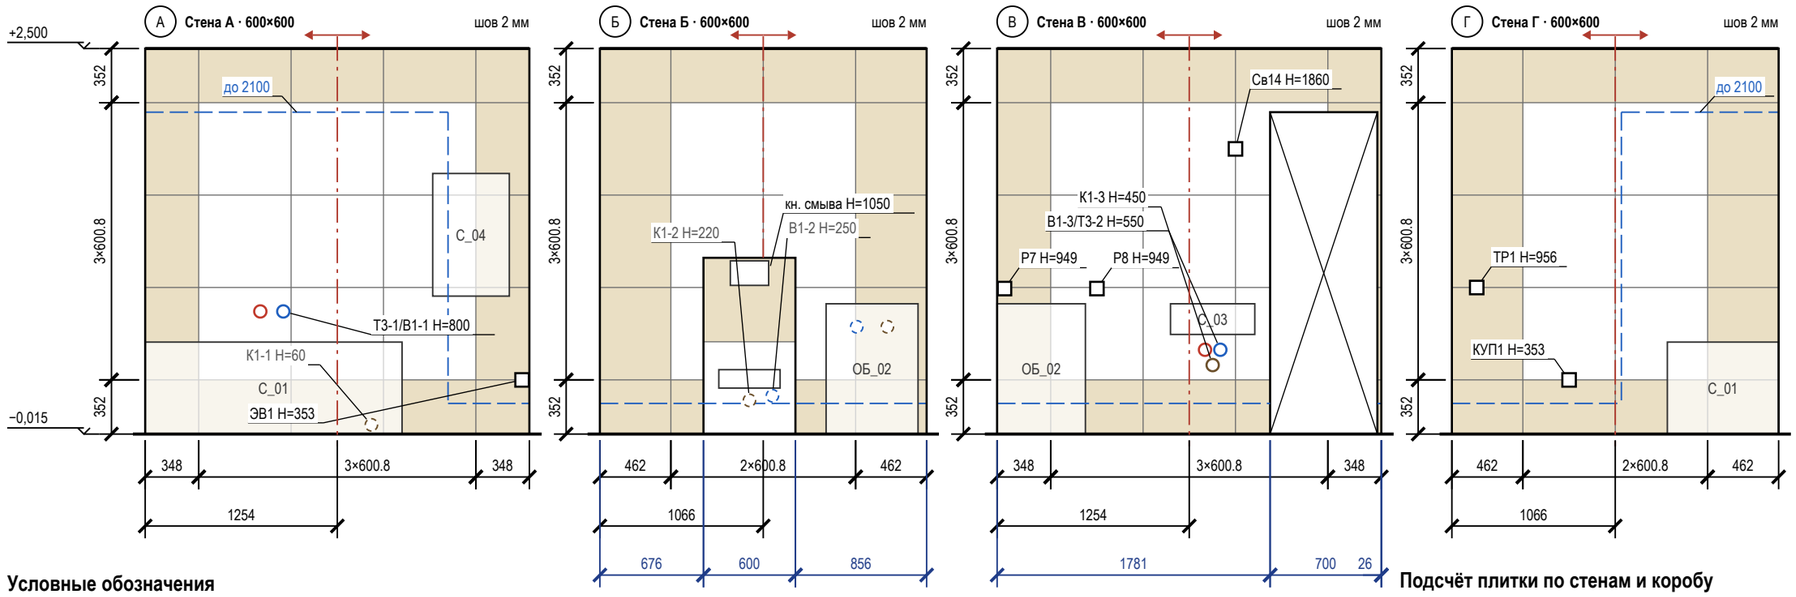


## Условные обозначения

- плитка целая; тонкая линия — шов
- плитка с подрезкой (размер — на цепочке)
- ось старта; стрелки — направление укладки
- верх гидроизоляции: 200 от ЧП, в мокрой зоне — «до …»
- проём — не облицовывается
- сантехприбор: габарит, высота по практике
- короб инсталляции, в нём кнопка смыва 250×160
- вывод В1 (код — в ведомости привязок)
- вывод Т3 (код — в ведомости привязок)
- вывод К1 (код — в ведомости привязок)
- вывод за прибором / в коробе (не на сетке)
- электроточка: марка и Н — по листам ЭОМ
- отметка уровня, м: ±0,000 — чистый пол жилых помещений
- низ потолка; серая полоса — стена без плитки
- (А) обозначение стены А–Г (как на развёртках)


## Подсчёт плитки по стенам и коробу

| Поверхность | L × H, мм | S, м² | Целых | Подр. | С запасом | Подрезки: край / верх, мм |
|---|---|---|---|---|---|---|
| стена А | 2507 × 2515 | 6,43 | 9 | 16 | 28 | 348 / 348; 352 |
| стена Б | 2132 × 2515 | 4,79 | 2 | 18 | 22 | 462 / 462; 352 |
| короб (ст. Б) | 600×1150×230 | 1,36 | 1 | 6 | 8 | лицо 600; бок. 230 |
| стена В | 2507 × 2515 | 4,96 | 6 | 19 | 28 | 348 / 348; 352 |
| стена Г | 2132 × 2515 | 5,48 | 6 | 14 | 22 | 462 / 462; 352 |
| **Итого** | | **23,01** | **24** | **73** | **108** | |

## Примечания

1. Вид изнутри, стены по часовой стрелке А → Г. Высоты — от чистого пола (−0,015), отметки — от ±0,000. Раскладка от чистовых размеров (штукатурка 10 + клей 5 + плитка 9 мм), подрезки чистые; старт — от оси стены, ряды от середины (две подрезки).
2. Облицовка до потолка (+2,500).
3. Открытые выводы и электроточки — на шве или в центре плитки (допуск 10 мм; плитка от 900 мм по высоте — на шве или не ближе 60 мм к нему).
4. Выводы ВК стоят по оси прибора и с прибором не двигаются — привязки по «Плану выводов сантехники» без сдвига; вне сетки (Т3-1/В1-1, В1-3/Т3-2, К1-3) отверстие в плитке коронкой по той же привязке, плитку не сдвигать.
5. За приборами и в коробе (К1-1, В1-2, К1-2, В1-4, К1-4) — штриховым кольцом.
6. Гидроизоляция: 200 мм от ЧП по периметру; над ванной — до 2100 и 300 мм за борт (СП 29.13330.2011, п. 7.2 — на высоту замачивания); углы — лентой; акт скрытых работ, пролив.
7. Короб 600×1150×230: лицо 600 мм от оси кнопки смыва, боковины, полка; углы — запил 45° или профиль; за коробом плитку не кладут.
8. Наружные углы: ст. Б: 2 — запил 45°; ст. В: 2 — профиль.
9. Люки: Л1 (ст. Б, 600×600, нажимной) — кромки дверцы по швам сетки.

| | | | | | | |
|---|---|---|---|---|---|---|
| | | | | | Проект: Четырёхкомнатная квартира | **М 1:40** |
| | Лист | № док. | Подпись | Дата | Раскладка плитки. Ванная комната. Развёртки стен | Стадия / Лист / Листов |
| Дизайнер | Кырлан А.С. | | | 04.11.26 | | П / 32 / 120 |

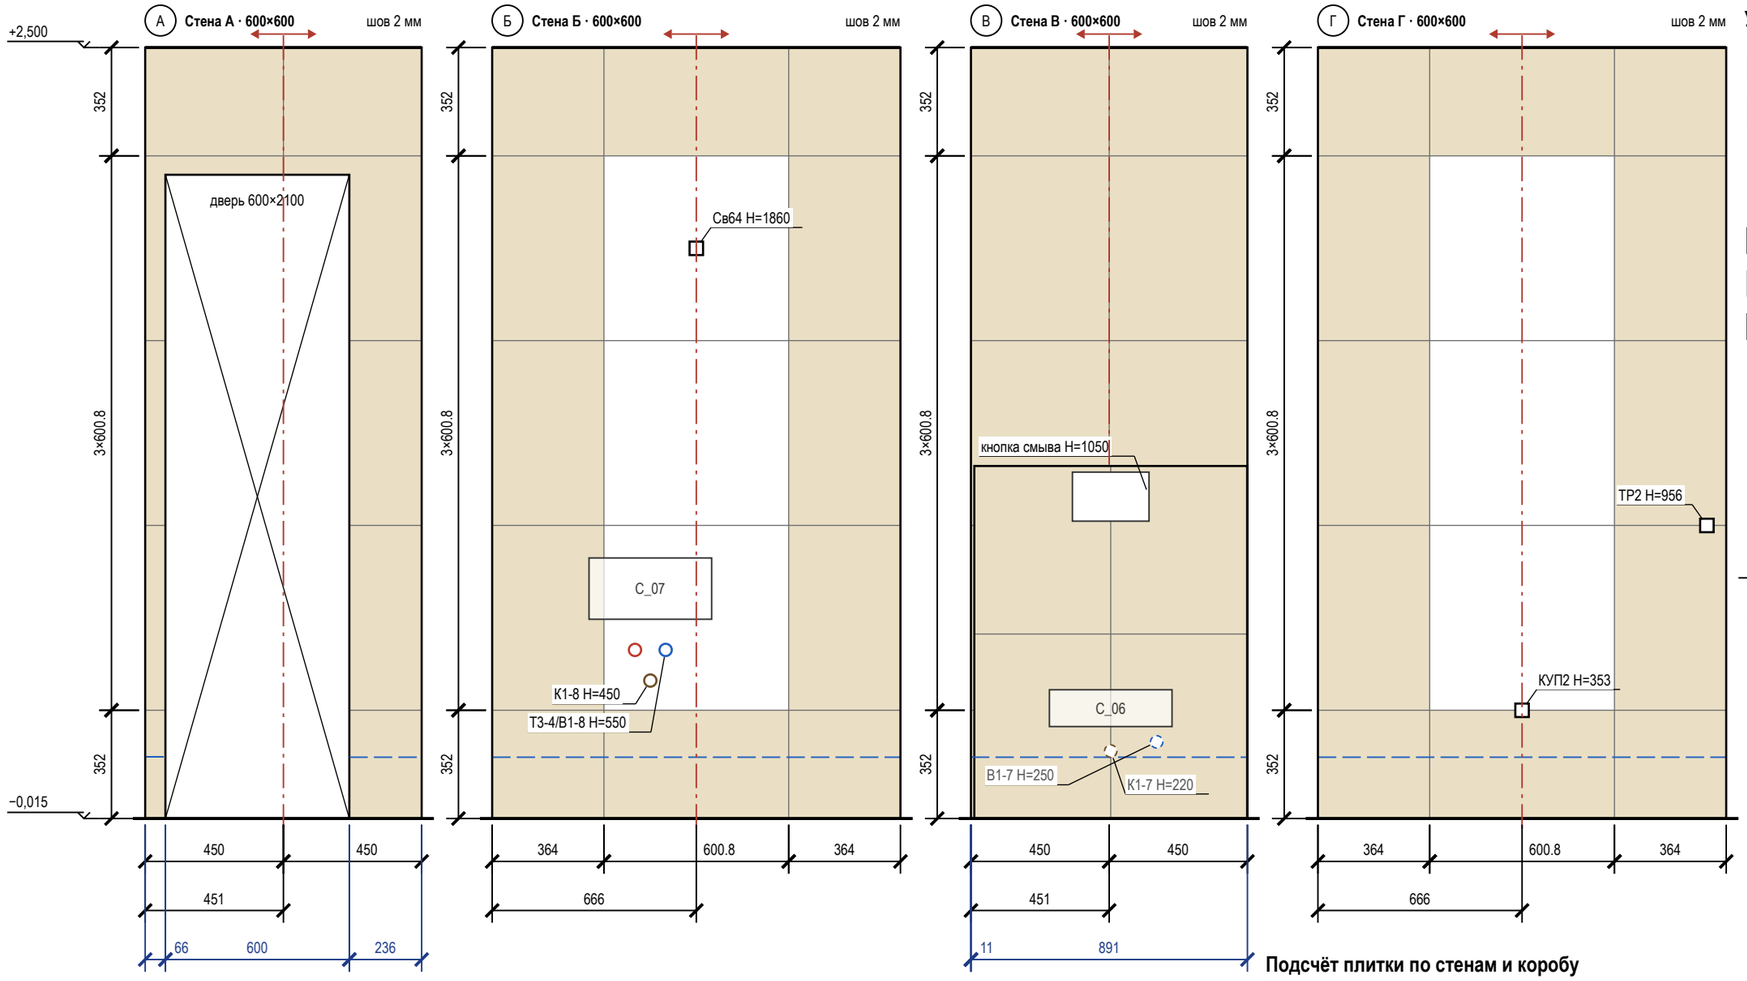


## Условные обозначения

- плитка целая; тонкая линия — шов
- плитка с подрезкой (размер — на цепочке)
- ось старта; стрелки — направление укладки
- верх гидроизоляции: 200 от ЧП, в мокрой зоне — «до …»
- проём — не облицовывается
- сантехприбор: габарит, высота по практике
- короб инсталляции, в нём кнопка смыва 250×160
- вывод В1 (код — в ведомости привязок)
- вывод Т3 (код — в ведомости привязок)
- вывод К1 (код — в ведомости привязок)
- вывод за прибором / в коробе (не на сетке)
- электроточка: марка и Н — по листам ЭОМ
- отметка уровня, м: ±0,000 — чистый пол жилых помещений
- низ потолка; серая полоса — стена без плитки
- (А) обозначение стены А–Г (как на развёртках)


## Подсчёт плитки по стенам и коробу

| Поверхность | L × H, мм | S, м² | Целых | Подр. | С запасом | Подрезки: край / верх, мм |
|---|---|---|---|---|---|---|
| стена А | 902 × 2515 | 1,13 | 0 | 10 | 11 | 450 / 450; 352 |
| стена Б | 1332 × 2515 | 3,47 | 3 | 12 | 17 | 364 / 364; 352 |
| стена В | 902 × 2515 | 1,37 | 0 | 10 | 11 | 450 / 450; 352 |
| короб (ст. В) | 890×1150×230 | 1,76 | 0 | 10 | 11 | лицо 444 / 444; бок. 230 |
| стена Г | 1332 × 2515 | 3,47 | 3 | 12 | 17 | 364 / 364; 352 |
| **Итого** | | **11,19** | **6** | **54** | **67** | |

## Примечания

1. Вид изнутри, стены по часовой стрелке А → Г. Высоты — от чистого пола (−0,015), отметки — от ±0,000. Раскладка от чистовых размеров (штукатурка 10 + клей 5 + плитка 9 мм), подрезки чистые; старт — от оси стены, ряды от середины (две подрезки).
2. Облицовка до потолка (+2,500).
3. Открытые выводы и электроточки — на шве или в центре плитки (допуск 10 мм; плитка от 900 мм по высоте — на шве или не ближе 60 мм к нему).
4. Выводы ВК стоят по оси прибора и с прибором не двигаются — привязки по «Плану выводов сантехники» без сдвига; вне сетки (Т3-4/В1-8, К1-8) — отверстие в плитке коронкой по той же привязке, плитку не сдвигать.
5. За приборами и в коробе (В1-7, К1-7) — штриховым кольцом.
6. Гидроизоляция: 200 мм от ЧП по периметру; углы — лентой; акт скрытых работ, пролив.
7. Короб 890×1150×230: лицо 444 / 444 мм от оси кнопки смыва, боковины, полка; углы — запил 45° или профиль; за коробом плитку не кладут.
8. Между коробом и углом полоса 11 мм — довести короб до угла.
9. Наружные углы: ст. А: 2 — профиль.

| | | | | | | |
|---|---|---|---|---|---|---|
| | | | | | Проект: Четырёхкомнатная квартира | **М 1:20** |
| | Лист | № док. | Подпись | Дата | | |
| Дизайнер | Кырлан А.С. | | | 04.11.26 | Раскладка плитки. Санузел. Развёртки стен | |
| | | | | | Стадия: П | Лист: 33 / Листов: 120 |

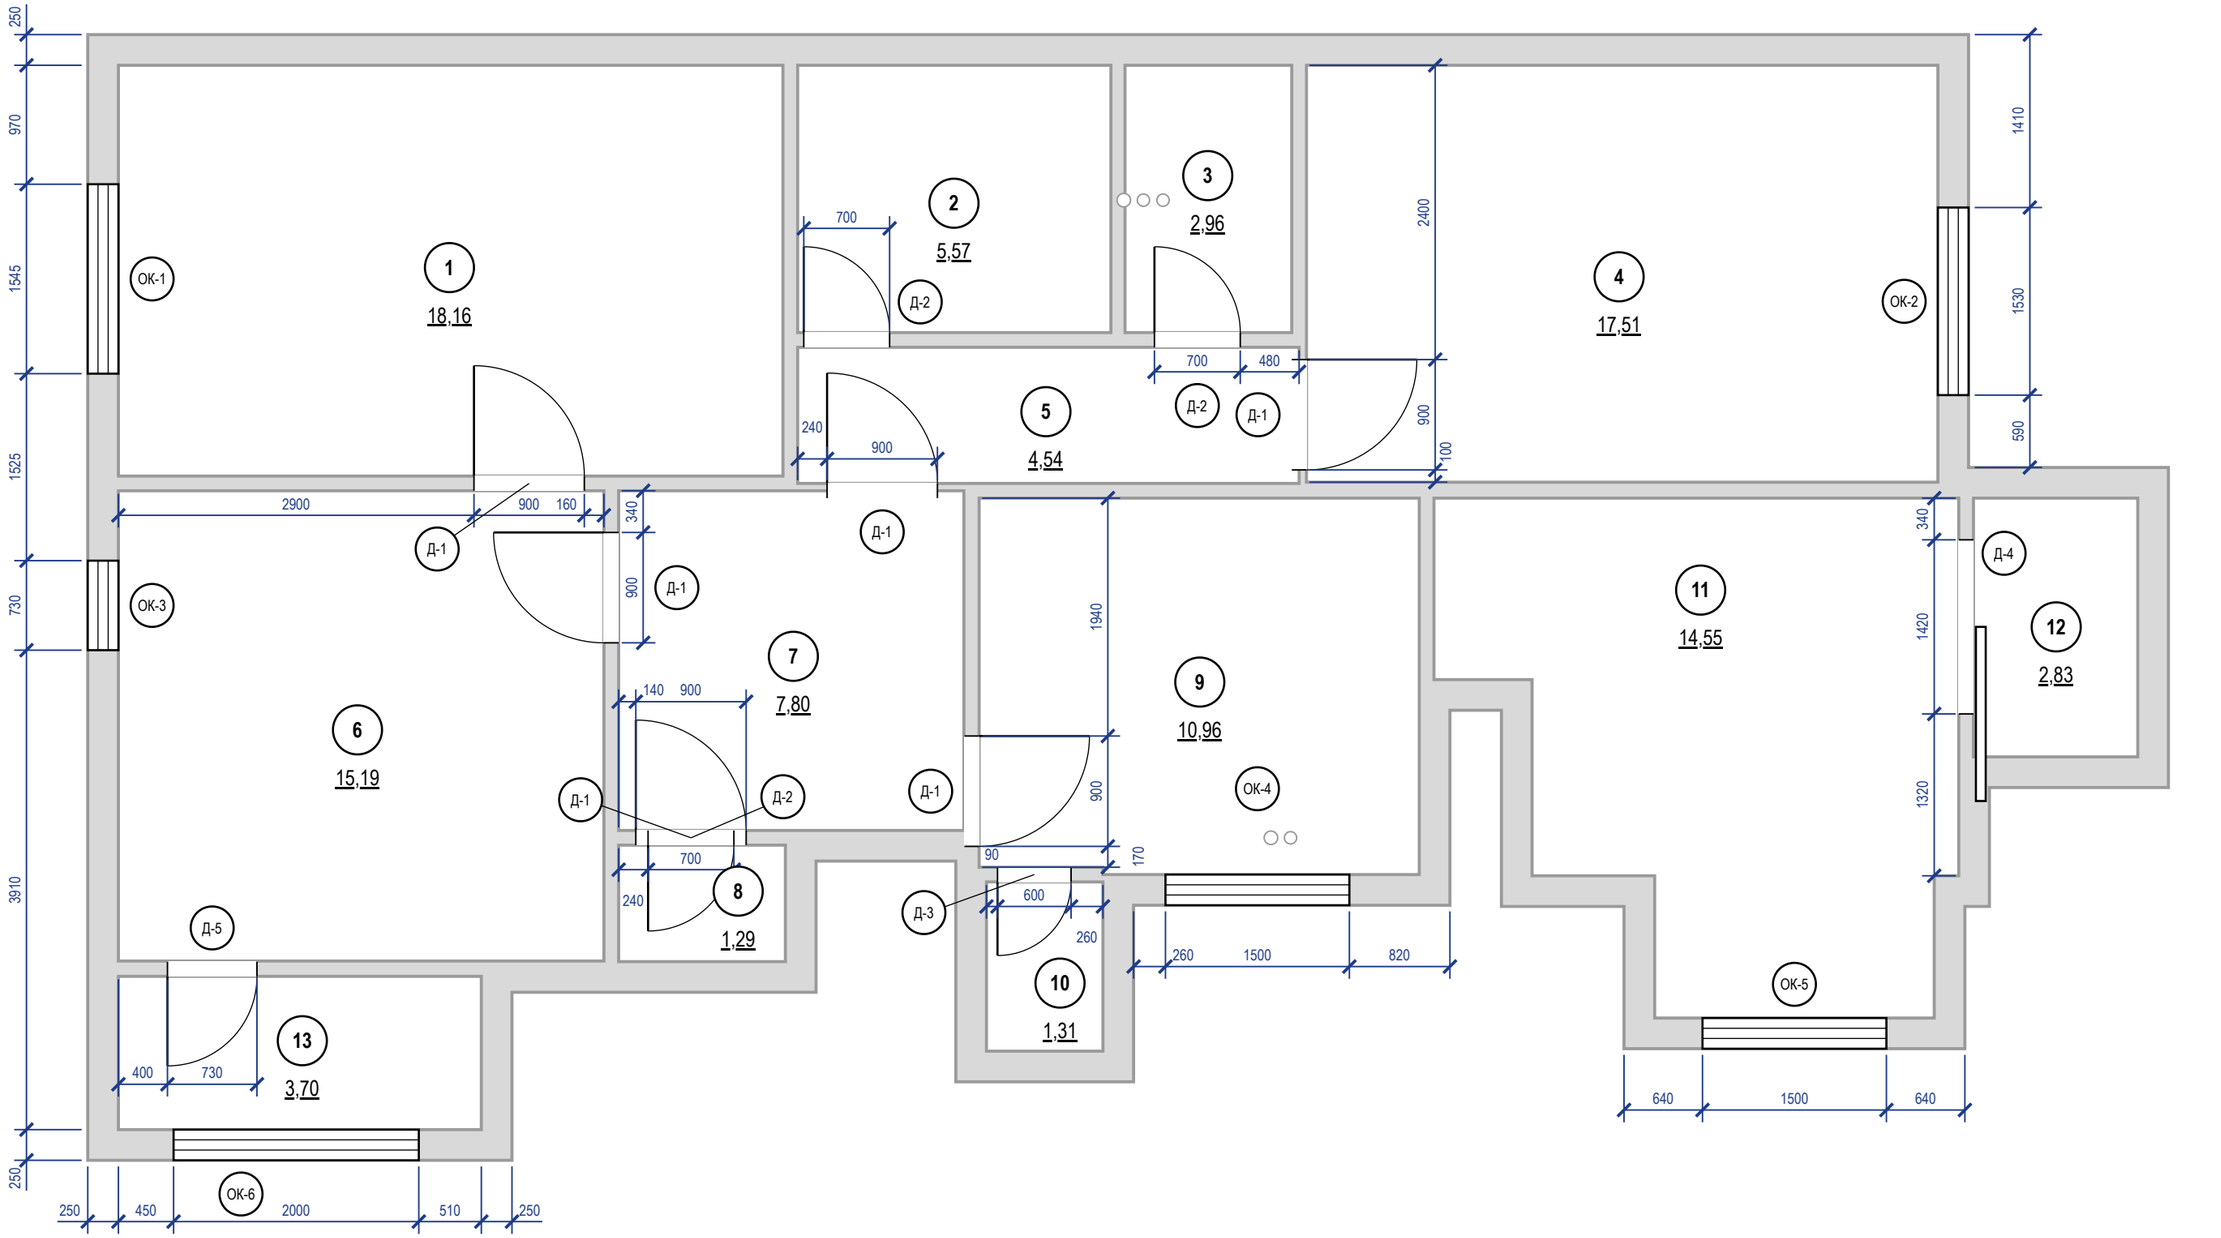


## Примечания


1. Размеры проёмов и привязки — в миллиметрах от чистых граней стен до отделки; привязка — от угла того помещения, со стороны которого стоит размер. Размер проёма — ширина × высота от чистого пола 0,000. Размеры на плане — проёмов, не полотен: полотно — в ведомости, коробка — по системе.
2. Марки в кружках — типы заполнения проёмов (ГОСТ 21.501-2018, п. 5.3.2); одна марка — один типоразмер; количество сверено с планом.
3. Размеры проёмов и привязки сняты со скана плана заказчика и на объекте не замерены (обмерный план — лист 6).
4. Экспликация помещений — лист 6; в марках помещений — номер и площадь, м².
5. Ведомость заполнения проёмов, открывание полотен, заказ и порядок монтажа блоков — лист 35.
6. Привязка проёма к углу помещения меньше 1 мм на листе, размер на плане не показан: Д-2 — 50 мм.

| | | | | | | |
|---|---|---|---|---|---|---|
| | | | | | Проект: Четырёхкомнатная квартира | М 1:50 |
| | Лист | № док. | Подпись | Дата | | |
| Дизайнер | Кырлан А.С. | | | 04.11.26 | План размещения дверей | Стадия: П; Лист: 34; Листов: 120 |

## Ведомость заполнения проёмов

| Марка | Наименование, обозначение | Проём ш×в, мм | Полотно (расч.) | Кол. | Откр. | Отделка полотна | Фурнитура | Прим. |
|---|---|---|---|---|---|---|---|---|
| Д-1 | Блок дверной внутренний, ГОСТ 475-2016 | 900×2100 | 800×2000 | 6 | П, П, П, Л, П, П | | петли, ручка с защёлкой | пом. 5; б/п |
| Д-2 | Блок дверной внутренний, ГОСТ 475-2016 | 700×2100 | 600×2000 | 3 | П, П, Л | | петли, ручка с защёлкой, фиксатор WC | пом. 2; порог 15 |
| Д-3 | Блок дверной внутренний, ГОСТ 475-2016 | 600×2100 | не задано (записи реестра нет) | 1 | Л | | петли, ручка с защёлкой, фиксатор WC | порог 15 |
| Д-4 | Дверь раздвижная, ГОСТ 475-2016 | 1420×2100 | не задано (записи реестра нет) | 1 | | | раздвижная система, ручки-купе | пом. 12; б/п |
| Д-5 | Блок дверной внутренний, ГОСТ 475-2016 | 730×2100 | не задано (записи реестра нет) | 1 | Л | | петли, ручка с защёлкой | порог 30 |
| ОК-1 | Блок оконный, ГОСТ 23166-2021 | 1545×1600 | | 1 | | | | низ 800 |
| ОК-2 | Блок оконный, ГОСТ 23166-2021 | 1530×1600 | | 1 | | | | низ 800 |
| ОК-3 | Блок оконный, ГОСТ 23166-2021 | 730×1600 | | 1 | | | | низ 800 |
| ОК-4 | Блок оконный, ГОСТ 23166-2021 | 1500×1600 | | 1 | | | | пом. 9; низ 800 |
| ОК-5 | Блок оконный, ГОСТ 23166-2021 | 1500×1600 | | 1 | | | | пом. 11; низ 900 |
| ОК-6 | Блок оконный, ГОСТ 23166-2021 | 2000×1700 | | 1 | | | | низ 900 |


**Схемы дверных блоков (1:25) — вид со стороны открывания; вершина треугольника — сторона петель**

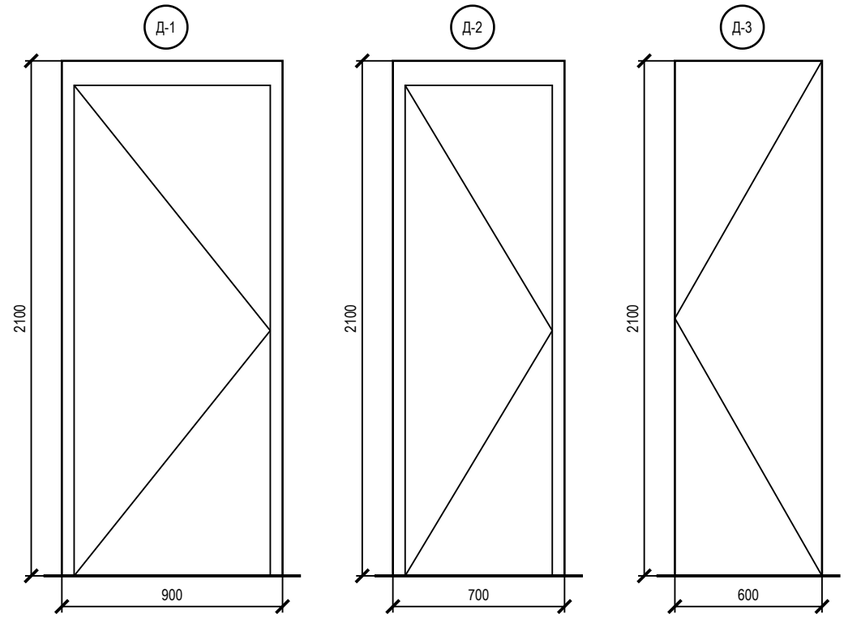


полотно 800×2000 (расч.)
откр. П, П, П, Л, П, П (схема — П, остальные по плану)

полотно 600×2000 (расч.)
откр. П, П, Л (схема — П, остальные по плану)

полотно не задано (записи реестра нет)
откр. Л

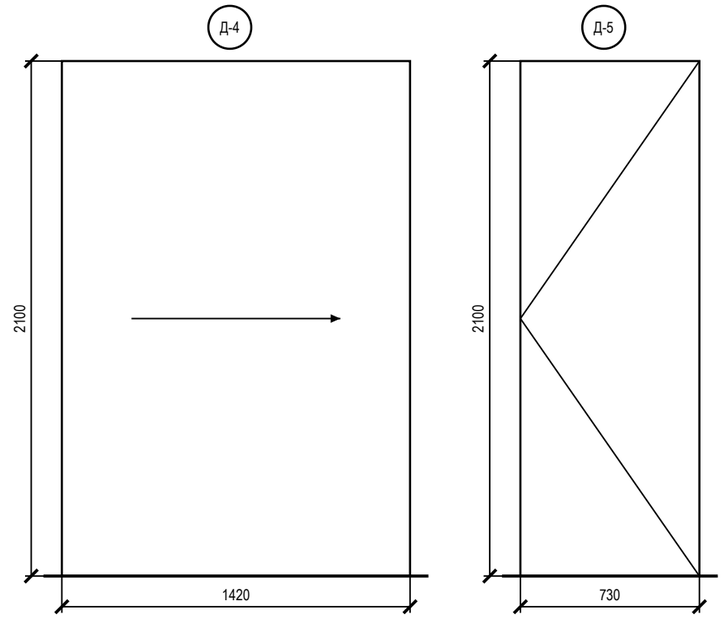


полотно не задано (записи реестра нет)
раздвижная


полотно не задано (записи реестра нет)
откр. Л

### Примечания

1. Марки проёмов — те же, что на плане размещения дверей (лист 34); привязки проёмов — там же.
2. Открывание: Л — петли слева, П — справа, если смотреть со стороны, куда открывается полотно (на себя).
3. Дверные блоки обычного монтажа (Д-1…Д-5) заказывать после чистовой стяжки и штукатурки, проёмы перемерить; монтажный зазор коробки 10–15 мм на сторону, откос от угла помещения до коробки — не менее 50 мм.
4. Полотно «расч.» — по проёму с запасом по каталогам, заказ — по таблице проёмов модели; Д-1, Д-2: проём 2100, а под полотно 2000 по каталогам нужен 2040–2080, под 2100 2140–2180: высоту проёма — по модели; Д-3: проём 600×2100 вне ряда стандартных полотен — полотно задать при выборе модели; Д-4: раздвижная, полотно — по системе — полотно задать при выборе модели; Д-5: проём 730×2100 вне ряда стандартных полотен — полотно задать при выборе модели.

| | | | | | |
|---|---|---|---|---|---|
| | | | | | Проект: Четырёхкомнатная квартира |
| | Лист | № док. | Подпись | Дата | |
| Дизайнер | Кырлан А.С. | | | 04.11.26 | Ведомость заполнения проёмов |

| Стадия | Лист | Листов |
|---|---|---|
| П | 35 | 120 |

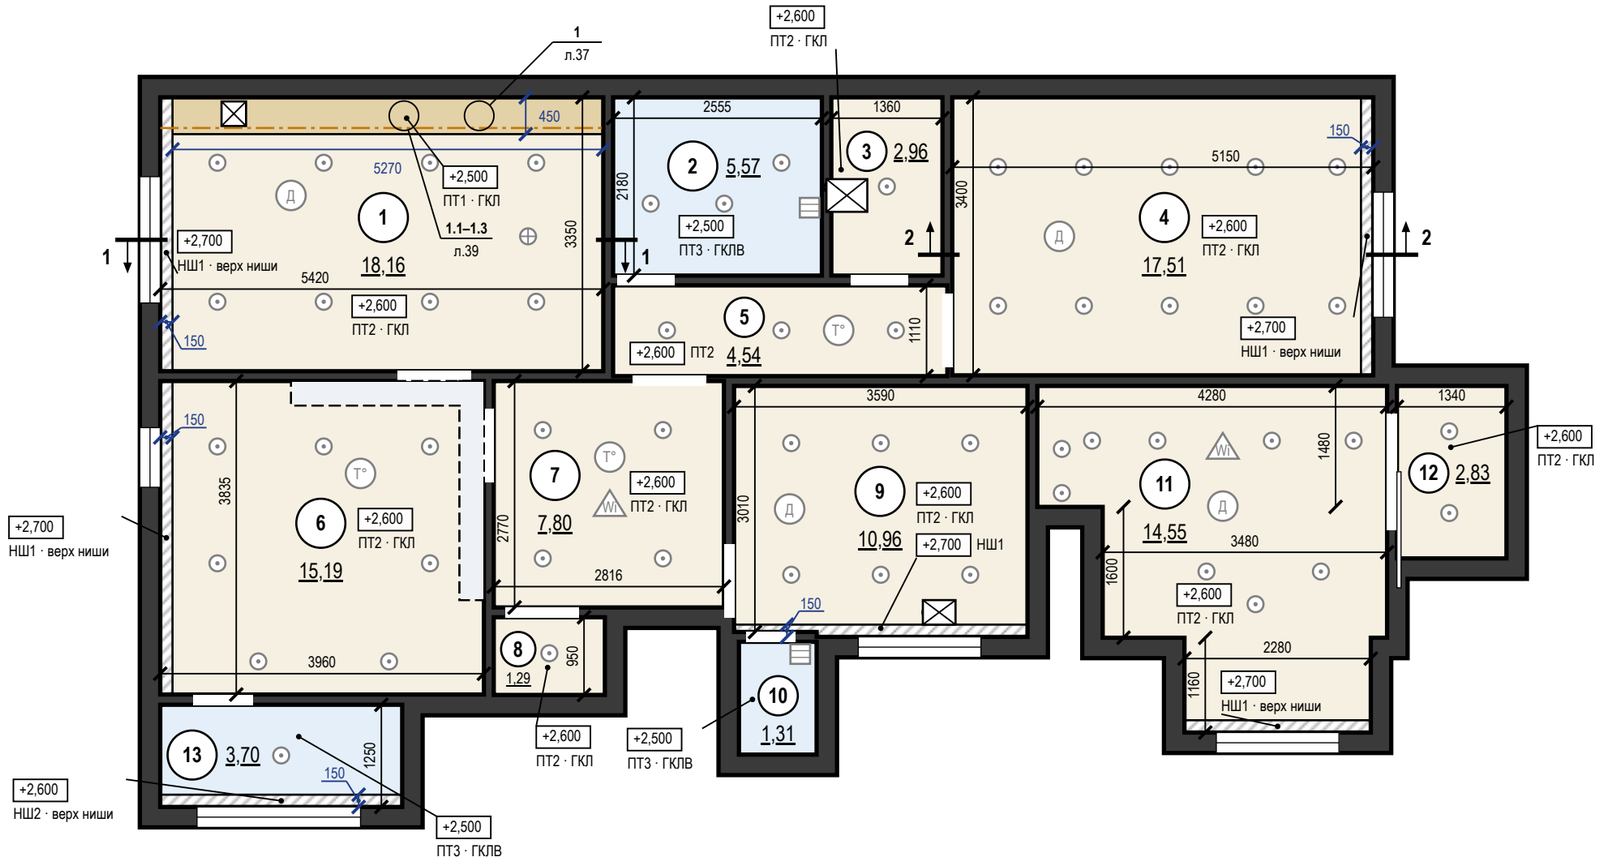


## Ведомость потолков

| Пом. | Марка | Конструкция | Низ / верх ниши | S, м² | Q |
|---|---|---|---|---|---|
| 1 | ПТ1 | ГКЛ П113, короб LED | +2,500 | 2,37 | Q3 |
| 1 | ПТ2 | ГКЛ П113 | +2,600 | 15,29 | Q3 |
| 1 | НШ1 | ниша под шторы 150×100 | +2,700 | 0,50 | |
| 2 | ПТ3 | ГКЛВ П113 | +2,500 | 5,57 | Q3 |
| 3 | ПТ2 | ГКЛ П113 | +2,600 | 2,96 | Q3 |
| 4 | ПТ2 | То же | +2,600 | 17,00 | Q3 |
| 4 | НШ1 | ниша под шторы 150×100 | +2,700 | 0,51 | |
| 5 | ПТ2 | ГКЛ П113 | +2,600 | 4,54 | Q3 |
| 6 | ПТ2 | То же | +2,600 | 14,61 | Q3 |
| 6 | НШ1 | ниша под шторы 150×100 | +2,700 | 0,58 | |
| 7 | ПТ2 | ГКЛ П113 | +2,600 | 7,80 | Q3 |
| 8 | ПТ2 | То же | +2,600 | 1,29 | Q3 |
| 9 | ПТ2 | То же | +2,600 | 10,48 | Q3 |
| 9 | НШ1 | ниша под шторы 150×100 | +2,700 | 0,48 | |
| 10 | ПТ3 | ГКЛВ П113 | +2,500 | 1,31 | Q3 |
| 11 | ПТ2 | ГКЛ П113 | +2,600 | 14,21 | Q3 |
| 11 | НШ1 | ниша под шторы 150×100 | +2,700 | 0,34 | |
| 12 | ПТ2 | ГКЛ П113 | +2,600 | 2,83 | Q3 |
| 13 | ПТ3 | ГКЛВ П113 | +2,500 | 3,26 | Q3 |
| 13 | НШ2 | ниша под шторы 150×100 | +2,600 | 0,44 | |
| | | **Итого** | | **106,37** | |

## Ведомость вырезов и закладных в потолке

| Марка | Устройство | Кол. | Пом. |
|---|---|---|---|
| | Светильник встраиваемый (марки — план освещения) | 56 | 1, 2, 3, 4, 5, 6, 7, 8, 9, 10, 11, 12, 13 |
| | Светильник подвесной (марки — план освещения) | 1 | 1 |
| ИП1, ИП2, ИП6, ИП7 | Извещатель дымовой | 4 | 1, 4, 9, 11 |
| ИП3…ИП5 | Извещатель тепловой | 3 | 5, 6, 7 |
| АР1, АР2 | Точка доступа Wi-Fi, PoE | 2 | 7, 11 |
| ВР1, ВР3 | Решётка вытяжная (вентилятор) | 2 | 2, 10 |
| | Люк ревизии 500×400, 400×300, 300×300 | 3 | 1, 3, 9 |

## Примечания


1. За отметку ±0,000 принят уровень чистого пола сухих помещений (готовое покрытие), а не существующего пола; пол пом. 2, 10, 13 — −0,015, −0,030; верх плиты перекрытия −0,170 — расчётный по пирогу пола, не замерен; существующий пол снимается до плиты, его отметка не замерена. Отметки в прямоугольниках — низ потолка; низ плиты +2,700, +2,600. Марка потолка — одна конструкция и отметка на весь альбом.
2. Размеры помещений в свету (ширина × длина, мм), не поместившиеся на плане: пом. 3 — 1360 × 2180; пом. 5 — 4090 × 1110; пом. 8 — 1360 × 950; пом. 9 — 3590 × 3010, 2580 × 60; пом. 10 — 950 × 1380; пом. 12 — 1340 × 2110; пом. 13 — 2960 × 1250.
3. Потолки ГКЛ — каркасная система П113: подвесы через 1000 (с запасом: СП 163, табл. 14 — до 1100 при 0,15 кН/м²), несущие профили через 500, основные через 1200 мм; листы — поперёк несущих профилей. В помещениях 2, 10, 13 — ГКЛВ на оцинкованном каркасе.
4. LED-лента в алюминиевом профиле посередине карниза короба шириной 450 мм (узел 1, лист 37); длина по плану: пом. 1 — 5,4 м (в плане освещения 5,4).
5. Ниши под шторы 150×100 мм — на всю длину стены с окном; карниз — на закладной до обшивки (узел 2, лист 37).
6. Примыкание к стенам: теневой шов 15 мм, техзазор 3 мм — пом. 1, по стенам, выровненным штукатуркой (узел 1); пом. 2, 3, 4, 5, 6, 7, 8, 9, 10, 11, 12, 13 — разделительная лента.
7. Светильники и потолочные устройства — подложка с планов освещения, слаботочных систем и вентиляции (положение — по ним); вырезы и закладные — по ведомости на листе, до обшивки; отверстия не совмещать с профилями, глубина корпуса светильника до 70 мм.
8. Разрезы 1–1, 2–2 — на листе 37; высоты мебели и дверных блоков сверены с низом потолка в разрезах.
9. Шпаклевание ГКЛ и условия приёмки — Q3: рассеянный дневной свет, осмотр с 2 м; боковой свет не оценивается.
10. Пом. 6: короб воздуховода кухонной вытяжки ГКЛ 300×200 мм (ширина от стены × высота), низ +2,500, длина 4,44 м — по трассе плана вентиляции, вдоль стен до входа в канал под воздуховод Ø125; каркас ПН 28×27 по стене и плите, ПП 60×27, лист ГКЛ 12,5.
11. Люки ревизии 500×400, 400×300, 300×300 мм — по центру блоков питания LED (ревизия, ревизия, блок питания LED БП1; координаты — план освещения).
12. Сечения потолков М 1:10: пом. 4 — 4.1, 4.2 (лист 39); пом. 6 — 4.1, 4.2 (лист 39); пом. 9 — 4.1, 4.2 (лист 39); пом. 11 — 4.1, 4.2 (лист 39); пом. 13 — 13.1, 13.2 (листы 39, 40).

| | | | | | |
|---|---|---|---|---|---|
| | | | | | Проект: Четырёхкомнатная квартира — **М 1:75** |
| | Лист | № док. | Подпись | Дата | |
| Дизайнер | Кырлан А.С. | | | 04.11.26 | План потолков |

| Стадия | Лист | Листов |
|---|---|---|
| П | 36 | 120 |


## Разрез 1–1 (М 1:40)

Пом. 1 Зал; линия разреза — план потолков, лист 36

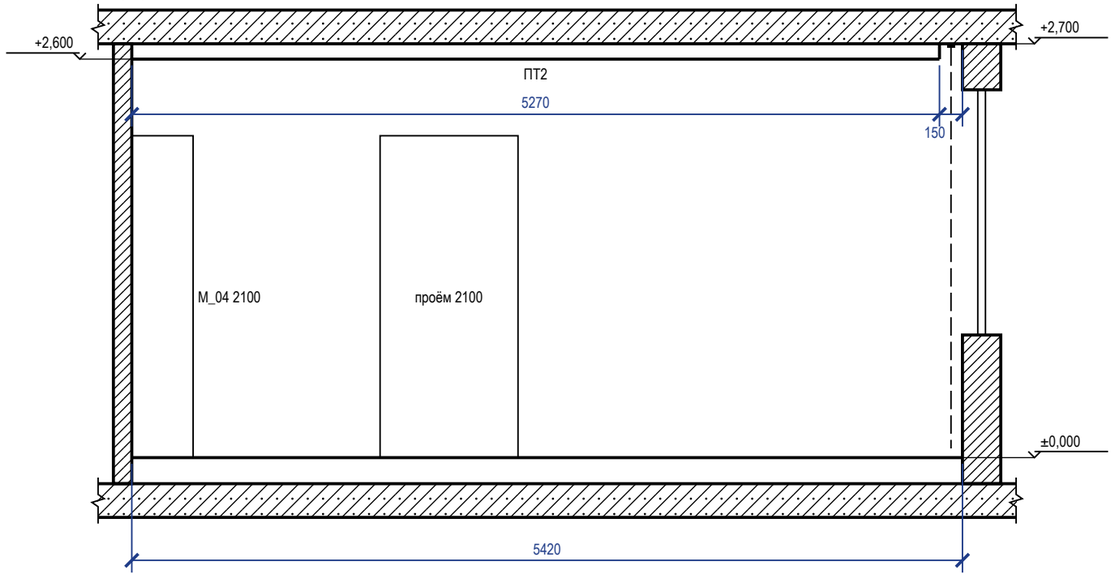



## Разрез 2–2 (М 1:40)

Пом. 4 Детская 1; линия разреза — план потолков, лист 36

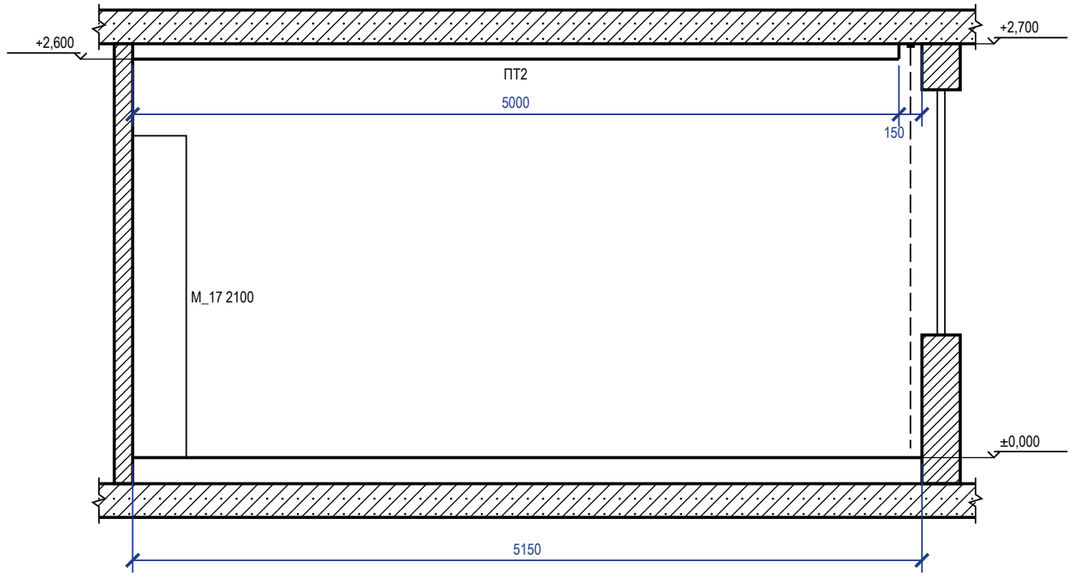


## 1 Короб с LED-подсветкой, теневой шов (М 1:10)


Пом. 1; карниз 150×100, щель под свет 60 мм

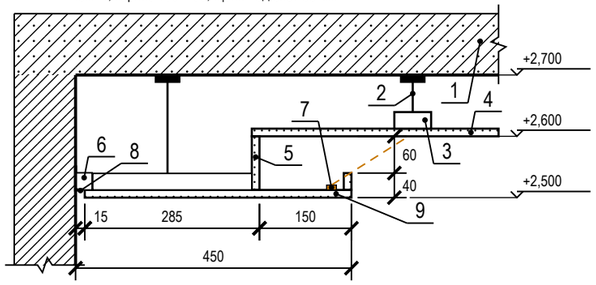


1 — плита перекрытия
2 — подвес прямой, шаг 1000 мм
3 — ПП 60×27: несущие через 500, основные через 1200 мм
4 — ГКЛ 12,5 по П113 — верхний уровень
5 — задняя стенка и бортик карниза — ГКЛ 12,5
6 — ПН 28×27 по периметру, к стене через 500 мм
7 — LED-лента в алюминиевом профиле
8 — теневой профиль: шов 15 мм, зазор 3 мм
9 — низ короба — ГКЛ 12,5 по ПП 60×27

## 2 Ниша под шторы (М 1:10)

Пом. 1, 4, 6, 9, 11, 13; без подсветки; закладные под карниз — до обшивки

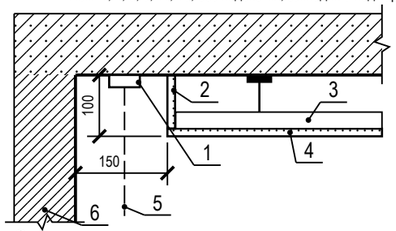


1 — карниз (шина), высота с верхом портьеры 80 мм
2 — стенка ниши — ГКЛ 12,5
3 — ПП 60×27 — каркас короба
4 — низ короба нижнего уровня — ГКЛ 12,5
5 — портьера
6 — стена с окном

### Отметки по помещениям, м

| Пом. | низ потолка | верх ниши | низ плиты |
|---|---|---|---|
| 1, 4, 6, 9, 11 | +2,600 | +2,700 | +2,700 |
| 13 | +2,500 | +2,600 | +2,600 |

### Условные обозначения

- плита перекрытия в сечении
- стена в сечении
- потолок ГКЛ в сечении; под линией — марка потолка (план потолков)
- мебель и дверные проёмы за секущей плоскостью; число — марка и верх от чистого пола, мм
- портьера в нише под шторы

### Примечания

1. Разрезы — по линиям 1–1, 2–2 на плане потолков (лист 36). Отметки — от ±0,000 чистого пола, м; размеры — мм.
2. Высоты мебели и дверных блоков за секущей плоскостью сверены с низом потолка над ними: верх ниже низа короба и поля.
3. ГКЛ 12,5 мм по каркасу П113; перепад уровней и бортик карниза — ГКЛ по ПП 60×27 (узел 1 — на этом листе). Ниша под шторы — на всю длину стены с окном, карниз на закладной до обшивки (узел 2 — на этом листе).
4. Толщины плит перекрытия и пирога пола показаны условно.
5. Сечения потолков по помещениям М 1:10 (отметки помещения, профили, подвесы, крепёж, изделия) — листы 39–40.
6. Ведомость объёмов потолков (лист ГКЛ, профиль, подвесы, лента, блоки питания, люки) — на листе 38.

| | | | | | | |
|---|---|---|---|---|---|---|
| | | | | | Проект: Четырёхкомнатная квартира | М 1:40; 1:10 |
| | Лист | № док. | Подпись | Дата | | |
| Дизайнер | Кырлан А.С. | | | 04.11.26 | Разрезы и узлы потолков | Стадия: П; Лист: 37; Листов: 120 |

## Ведомость объёмов потолков

| Позиция | Ед. | Кол. | Пом. |
|---|---|---|---|
| Лист ГКЛ 12,5 | м² | 98,99 | 1, 3, 4, 5, 6, 7, 8, 9, 11, 12 |
| Лист ГКЛВ 12,5 | м² | 10,88 | 2, 10, 13 |
| Борта и карнизы (входят в площади листов выше) | м² | 3,50 | 1, 4, 6, 9, 11, 13 |
| Профиль ПП 60×27 | м | 307,26 | 1, 2, 3, 4, 5, 6, 7, 8, 9, 10, 11, 12, 13 |
| Профиль ПН 28×27 | м | 198,10 | 1, 2, 3, 4, 5, 6, 7, 8, 9, 10, 11, 12, 13 |
| Подвес прямой | шт. | 102 | 1, 2, 3, 4, 5, 6, 7, 8, 9, 10, 11, 12, 13 |
| Анкер-клин к плите | шт. | 102 | 1, 2, 3, 4, 5, 6, 7, 8, 9, 10, 11, 12, 13 |
| Шуруп TN 3,5×25 | шт. | 2527 | 1, 2, 3, 4, 5, 6, 7, 8, 9, 10, 11, 12, 13 |
| Лента армирующая для швов | м | 131,84 | 1, 2, 3, 4, 5, 6, 7, 8, 9, 10, 11, 12, 13 |
| Шпаклёвка для швов | кг | 43,95 | 1, 2, 3, 4, 5, 6, 7, 8, 9, 10, 11, 12, 13 |
| Грунтовка (швы) | л | 10,99 | 1, 2, 3, 4, 5, 6, 7, 8, 9, 10, 11, 12, 13 |
| Лента разделительная по периметру | м | 143,31 | 1, 2, 3, 4, 5, 6, 7, 8, 9, 10, 11, 12, 13 |
| Сплошная шпаклёвка и окраска (площадь развёртки) | м² | 109,87 | 1, 2, 3, 4, 5, 6, 7, 8, 9, 10, 11, 12, 13 |
| Лента LED | м | 5,42 | 1 |
| Требуемая мощность блоков питания | Вт | 68 | 1 |
| Установленная мощность блоков питания | Вт | 100 | 1 |
| Блок питания LED | шт. | 1 | 1 |
| Люк ревизии | шт. | 3 | 1, 3, 9 |


## Примечания

1. ГКЛ 12,5 мм по каркасу П113; узлы коробов и ниш под шторы: узел 1 — лист 37; узел 2 — лист 37; условные обозначения разрезов — на листе 37.
2. Ведомость объёмов — по геометрии плана потолков: Лист ГКЛ 12,5 — плоскости уровней + борта (без арочных участков); Лист ГКЛВ 12,5 — плоскости уровней + борта; Борта и карнизы — длина перепада × перепад; Профиль ПП 60×27 — S × (1/шаг несущ. + 1/шаг осн.) + стойки бортов; Профиль ПН 28×27 — периметр стен + 2 × перепады + карнизы; Подвес прямой — по раскладке: S уровня / (шаг осн. × шаг подвесов), пояс уже шага — ряд вдоль пояса, фигура — по контуру; шаг подвесов — не больше табл. 14 СП 163; Анкер-клин к плите — по одному на подвес (Knauf П113); Шуруп TN 3,5×25 — 23 шт./м² (Knauf П113, табл. 2 альбома П 11); Лента армирующая для швов — 1,2 м/м² листа (Knauf); Шпаклёвка для швов — 0,4 кг/м² листа, только швы (Knauf); Грунтовка (швы) — 0,1 л/м² листа, только швы (Knauf); Лента разделительная по периметру — периметр стен под потолком ГКЛ; Сплошная шпаклёвка и окраска (площадь развёртки) — плоскости + борта; расход — по паспорту материала (норма расхода на сплошной слой не подтверждена); Лента LED — по оси карниза и ниши фигуры (план потолков); Требуемая мощность блоков питания — Вт/м × длина × 1,3; Установленная мощность блоков питания — сумма мощностей блоков по плану освещения; Блок питания LED — блоки потолочных лент по плану освещения (БП1); Люк ревизии — план потолков; без запаса на подрезку (при закупке листа: ×1,075 при S > 20 м², ×1,175 — 10–20 м², ×1,275 — < 10 м²).

| | | | | | |
|---|---|---|---|---|---|
| | | | | | Проект: Четырёхкомнатная квартира |
| | Лист | № док. | Подпись | Дата | |
| Дизайнер | Кырлан А.С. | | | 04.11.26 | Разрезы и узлы потолков (продолжение) |
| | | | | | Стадия: П; Лист: 38; Листов: 120 |

## Сечение 1.1. Короб с LED-подсветкой, теневой шов (М 1:10)


Пом. 1 Зал; карниз 150×100, щель под свет 60 мм

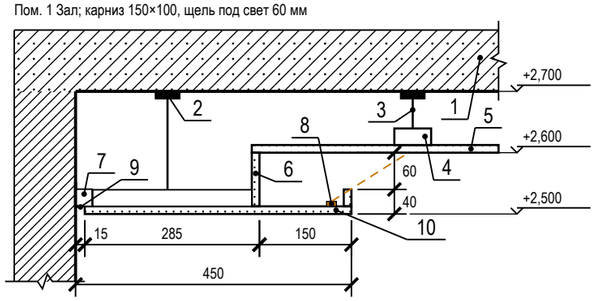


1 — плита перекрытия
2 — анкер-клин к плите — по одному на подвес
3 — подвес прямой, шаг 1000 мм
4 — ПП 60×27: несущие через 500, основные через 1200 мм; соединители одноуровневые, шурупы LN 3,5×9
5 — ГКЛ 12,5 по П113 — верхний уровень; шурупы TN 3,5×25 через 170 мм
6 — задняя стенка и бортик карниза — ГКЛ 12,5
7 — ПН 28×27 по периметру — дюбель-гвоздь через ≤ 500 мм, не менее 3 на профиль
8 — LED-лента 9,6 Вт/м, 24 В в алюминиевом профиле
9 — теневой профиль: шов 15 мм, зазор 3 мм
10 — низ короба — ГКЛ 12,5 по ПП 60×27

## Сечение 1.2. Ниша под шторы (М 1:10)


Пом. 1 Зал; без подсветки; закладные под карниз — до обшивки

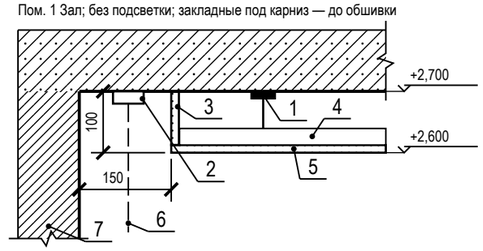


1 — анкер-клин к плите — по одному на подвес; подвес прямой, шаг 1000 мм
2 — карниз (шина), высота с верхом портьеры 80 мм
3 — стенка ниши — ГКЛ 12,5
4 — ПП 60×27 — каркас короба, основные через 1200 мм; соединители одноуровневые, шурупы LN 3,5×9
5 — низ короба нижнего уровня — ГКЛ 12,5; шурупы TN 3,5×25 через 170 мм
6 — портьера
7 — стена с окном

## Сечение 1.3. Примыкание потолка к стене (М 1:10)


Пом. 1 Зал; примыкание — разделительная лента

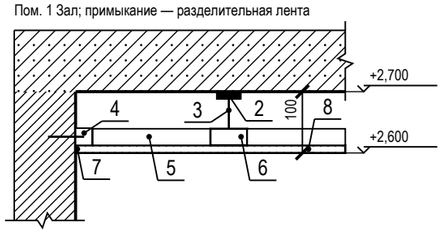


1 — плита перекрытия
2 — анкер-клин к плите — по одному на подвес
3 — подвес прямой, шаг 1000 мм
4 — ПН 28×27 по периметру — дюбель-гвоздь через ≤ 500 мм, не менее 3 на профиль
5 — ПП 60×27 несущий (вид) через 500 мм, в ПН
6 — ПП 60×27 основной (сечение) через 1200 мм; соединители одноуровневые, шурупы LN 3,5×9
7 — лента разделительная по стене, шов зашпаклёван
8 — ГКЛ 12,5 по П113; шурупы TN 3,5×25 через 170 мм

## Сечение 4.1. Ниша под шторы (М 1:10)


Пом. 4 Детская 1, 6 Кухня, 9 Детская 2, 11 Гостиная; без подсветки; закладные под карниз — до обшивки

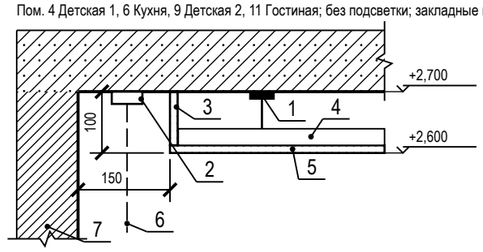


1 — анкер-клин к плите — по одному на подвес; подвес прямой, шаг 1000 мм
2 — карниз (шина), высота с верхом портьеры 80 мм
3 — стенка ниши — ГКЛ 12,5
4 — ПП 60×27 — каркас короба, основные через 1200 мм; соединители одноуровневые, шурупы LN 3,5×9
5 — низ короба нижнего уровня — ГКЛ 12,5; шурупы TN 3,5×25 через 170 мм
6 — портьера
7 — стена с окном

## Сечение 4.2. Примыкание потолка к стене (М 1:10)


Пом. 4 Детская 1, 6 Кухня, 9 Детская 2, 11 Гостиная; примыкание — разделительная лента

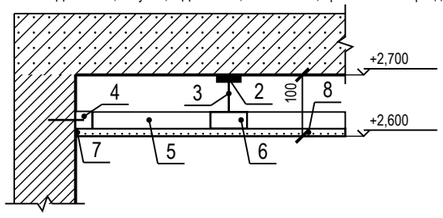


1 — плита перекрытия
2 — анкер-клин к плите — по одному на подвес
3 — подвес прямой, шаг 1000 мм
4 — ПН 28×27 по периметру — дюбель-гвоздь через ≤ 500 мм, не менее 3 на профиль
5 — ПП 60×27 несущий (вид) через 500 мм, в ПН
6 — ПП 60×27 основной (сечение) через 1200 мм; соединители одноуровневые, шурупы LN 3,5×9
7 — лента разделительная по стене, шов зашпаклёван
8 — ГКЛ 12,5 по П113; шурупы TN 3,5×25 через 170 мм

## Сечение 13.1. Ниша под шторы (М 1:10)

Пом. 13 Балкон 1; без подсветки; закладные под карниз — до обшивки

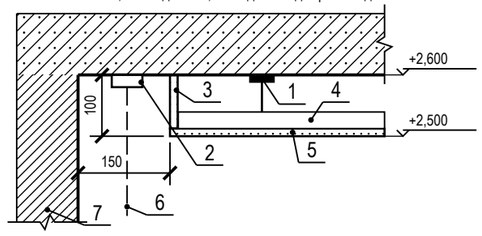


1 — анкер-клин к плите — по одному на подвес; подвес прямой, шаг 1000 мм
2 — карниз (шина), высота с верхом портьеры 80 мм
3 — стенка ниши — ГКЛВ 12,5
4 — ПП 60×27 — каркас короба, основные через 1200 мм; соединители одноуровневые, шурупы LN 3,5×9
5 — низ короба нижнего уровня — ГКЛВ 12,5; шурупы TN 3,5×25 через 170 мм
6 — портьера
7 — стена с окном

## Условные обозначения

— · — LED-лента в нише подсветки (карниз короба, ниша фигуры)


## Примечания

1. Сечения потолков М 1:10 по помещениям с нишами LED и нишами под шторы: отметки и размеры этого помещения от ±0,000 чистого пола (м, мм). Положение — по плану потолков (лист 36): короб и ниша LED — по линиям ленты, ниша под шторы — у стены с окном; типовые узлы по группам помещений — на листе 37.
2. Крепёж: подвес прямой к плите на анкер-клине — по одному на подвес (Knauf П113); ПН к стенам — дюбель-гвоздь через ≤ 500 мм, не менее 3 на профиль (серия 1.045.9-2.08); лист 12,5 — шурупы TN 3,5×25 через 170 мм (СП 163, табл. 15); профили между собой — соединители одноуровневые, шурупы LN 3,5×9.
3. Изделие карниза, профиля LED и галтели подписано артикулом из данных; где артикул не выбран, сечение дано по габаритам из данных (ширина и глубина ниши, щель под свет), изделие подбирается по ним.

| | | | | | Проект: Четырёхкомнатная квартира | | | **М 1:10** |
|---|---|---|---|---|---|---|---|---|
| | Лист | № док. | Подпись | Дата | Сечения потолков М 1:10 | Стадия | Лист | Листов |
| Дизайнер | Кырлан А.С. | | | 04.11.26 | | П | 39 | 120 |

## Сечение 13.2. Примыкание потолка к стене (М 1:10)

Пом. 13 Балкон 1; примыкание — разделительная лента

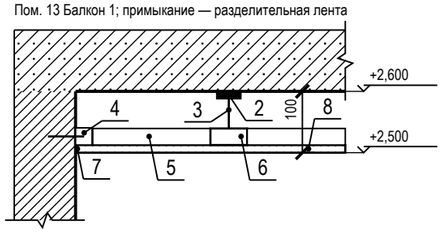


1 — плита перекрытия

2 — анкер-клин к плите — по одному на подвес

3 — подвес прямой, шаг 1000 мм

4 — ПН 28×27 по периметру — дюбель-гвоздь через ≤ 500 мм, не менее 3 на профиль

5 — ПП 60×27 несущий (вид) через 500 мм, в ПН

6 — ПП 60×27 основной (сечение) через 1200 мм; соединители одноуровневые, шурупы LN 3,5×9


7 — лента разделительная по стене, шов зашпаклёван

8 — ГКЛВ 12,5 по П113; шурупы TN 3,5×25 через 170 мм

### Примечания

1. Сечения потолков М 1:10 по помещениям с нишами LED и нишами под шторы: отметки и размеры этого помещения от ±0,000 чистого пола (м, мм). Положение — по плану потолков (лист 36): короб и ниша LED — по линиям ленты, ниша под шторы — у стены с окном; типовые узлы по группам помещений — на листе 37.
2. Крепёж: подвес прямой к плите на анкер-клине — по одному на подвес (Knauf П113); ПН к стенам — дюбель-гвоздь через ≤ 500 мм, не менее 3 на профиль (серия 1.045.9-2.08); лист 12,5 — шурупы TN 3,5×25 через 170 мм (СП 163, табл. 15); профили между собой — соединители одноуровневые, шурупы LN 3,5×9.
3. Изделия карнизов, профилей LED и галтелей — по артикулу из данных.

| | | | | | | |
|---|---|---|---|---|---|---|
| | | | | | Проект: Четырёхкомнатная квартира | М 1:10 |
| | Лист | № док. | Подпись | Дата | | |
| Дизайнер | Кырлан А.С. | | | 04.11.26 | Сечения потолков М 1:10 | Стадия: П; Лист: 40; Листов: 120 |

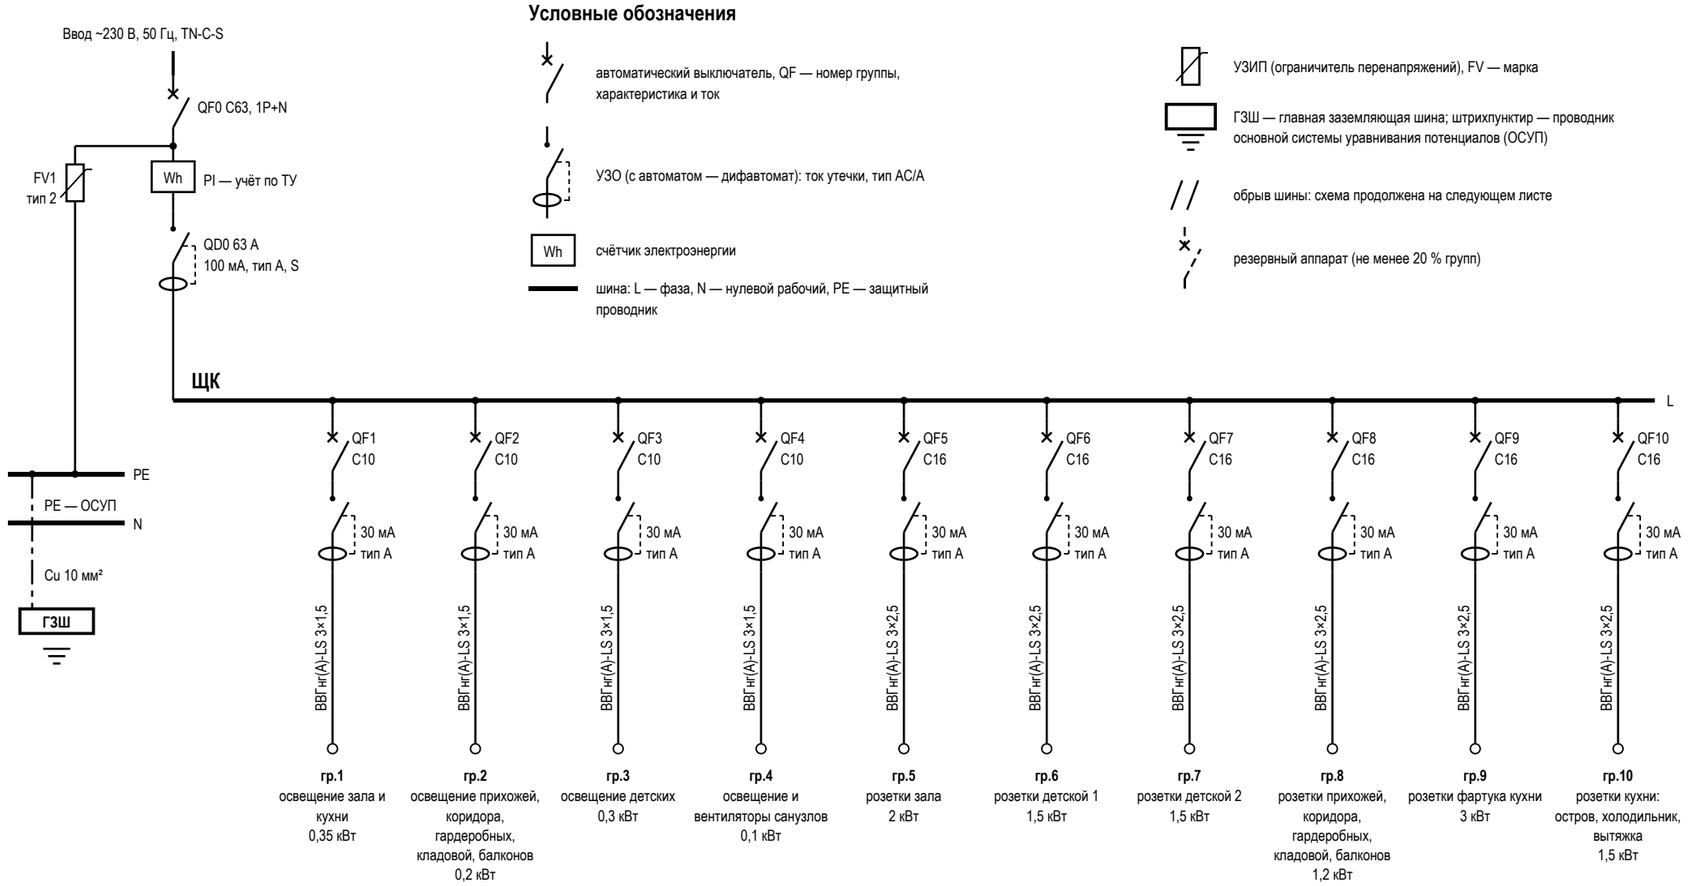


## Условные обозначения

- автоматический выключатель, QF — номер группы, характеристика и ток
- УЗО (с автоматом — дифавтомат): ток утечки, тип AC/A
- Wh — счётчик электроэнергии
- шина: L — фаза, N — нулевой рабочий, PE — защитный проводник
- УЗИП (ограничитель перенапряжений), FV — марка
- ГЗШ — главная заземляющая шина; штрихпунктир — проводник основной системы уравнивания потенциалов (ОСУП)
- обрыв шины: схема продолжена на следующем листе
- резервный аппарат (не менее 20 % групп)

## Данные щитка

| Показатель | Значение |
|---|---|
| Номер щитка | ЩК |
| Тип | ЩРВ-П-72, IP41, навесной |
| Уст. мощность, кВт | 29,75 |
| Разреш. мощность, кВт | 15 |
| Расчётная, кВт | 11,2 |
| Автоматы 1п: занят. / рез. | 19 / 4 |
| Модулей: всего / занято | 72 / 44 |
| Ток на вводе, А | 63 |
| Вводной аппарат | QF0 C63, 1P+N |
| УЗИП | FV1, тип 2, ЩК, после счётчика |
| ГЗШ, проводник ОСУП | Cu 10 мм² |
| Листов схемы | 2 (группы по листам) |

## Таблица групп щита ЩК и кабельный журнал


| № | Назначение | Помещения | Автомат | УЗО / дифавтомат | Кабель | Длина, м | Р, кВт | Точек |
|---|---|---|---|---|---|---|---|---|
| 1 | освещение зала и кухни | 1, 6 | C10 | 30 мА, тип A | ВВГнг(A)-LS 3×1,5 | 55,5 | 0,35 | 25 |
| 2 | освещение прихожей, коридора, гардеробных, кладовой, балконов | 3, 5, 6, 7, 8, 12, 13 | C10 | 30 мА, тип A | ВВГнг(A)-LS 3×1,5 | 111,7 | 0,2 | 20 |
| 3 | освещение детских | 4, 9, 11 | C10 | 30 мА, тип A | ВВГнг(A)-LS 3×1,5 | 99,5 | 0,3 | 34 |
| 4 | освещение и вентиляторы санузлов | 2, 5, 10 | C10 | 30 мА, тип A | ВВГнг(A)-LS 3×1,5 | 34,7 | 0,1 | 9 |
| 5 | розетки зала | 1 | C16 | 30 мА, тип A | ВВГнг(A)-LS 3×2,5 | 27,6 | 2 | 6 |
| 6 | розетки детской 1 | 4 | C16 | 30 мА, тип A | ВВГнг(A)-LS 3×2,5 | 32,8 | 1,5 | 5 |
| 7 | розетки детской 2 | 9 | C16 | 30 мА, тип A | ВВГнг(A)-LS 3×2,5 | 24,1 | 1,5 | 4 |
| 8 | розетки прихожей, коридора, гардеробных, кладовой, балконов | 3, 5, 7, 12, 13 | C16 | 30 мА, тип A | ВВГнг(A)-LS 3×2,5 | 72,9 | 1,2 | 6 |
| 9 | розетки фартука кухни | 6 | C16 | 30 мА, тип A | ВВГнг(A)-LS 3×2,5 | 18,3 | 3 | 4 |
| 10 | розетки кухни: остров, холодильник, вытяжка | 6 | C16 | 30 мА, тип A | ВВГнг(A)-LS 3×2,5 | 19,6 | 1,5 | 6 |

## Примечания

1. Схема однолинейная: одна линия — фаза, N и PE группы; аппараты — в отключённом положении (ГОСТ 2.702, ГОСТ 2.755). Номера групп — как у точек на планах (гр.). За отметку 0,000 принят уровень чистого пола; высота щита — по плану розеток.
2. Розеточные и мокрые линии — через УЗО или дифавтомат с током утечки не более 30 мА (ПУЭ 7.1.79); в санузле выполнить ДСУП (ПУЭ 7.1.87–7.1.88).
3. УЗО тип A — для линий с электроникой, стиральной и посудомоечной машиной, LED-драйверами; тип AC — только для чисто активной нагрузки.
4. Кабель — медный, исполнение нг(A)-LS (ГОСТ 31565-2012); скрытая прокладка только горизонтально и вертикально, фактические трассы зафиксировать исполнительной схемой до закрытия отделкой.
5. Номинал автомата — не выше допустимого тока кабеля: 1,5 мм² — до 10 А, 2,5 мм² — до 16 А. Резерв щита — не менее 20 % модулей.
6. Расчёт нагрузок, токов КЗ, селективности и сечений — по проекту ЭОМ организации с допуском СРО; лист задаёт состав, расположение и группы.
7. УЗИП FV1 — после вводного автомата, проводник к шине PE — кратчайший, без петель. Шина PE щита соединяется с ГЗШ проводником ОСУП; к ГЗШ присоединяются трубы водопровода и отопления на вводе в квартиру (ПУЭ 7.1.87). Шины N и PE — раздельные, после разделения PEN не объединяются.
8. До подключения нагрузки — приёмо-сдаточные испытания с протоколом: сопротивление изоляции линий не менее 0,5 МОм, срабатывание УЗО по току и времени, непрерывность защитных проводников PE (ПУЭ, гл. 1.8).

| | | | | | Проект: Четырёхкомнатная квартира | | | |
|---|---|---|---|---|---|---|---|---|
| | Лист | № док. | Подпись | Дата | Однолинейная схема щита | Стадия | Лист | Листов |
| Дизайнер | Кырлан А.С. | | | 04.11.26 | | П | 41 | 120 |

Продолжение однолинейной схемы щита ЩК, начало — лист 41

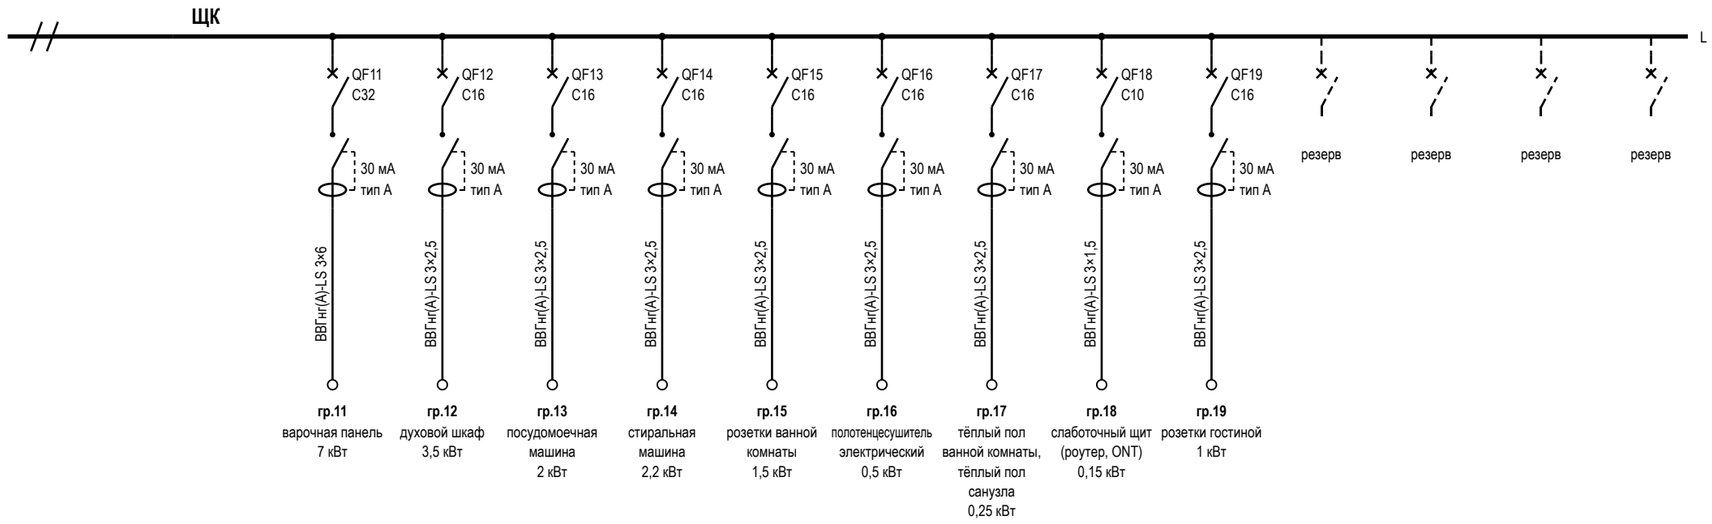



## Таблица групп щита ЩК и кабельный журнал (продолжение)

| № | Назначение | Помещения | Автомат | УЗО / дифавтомат | Кабель | Длина, м | Р, кВт | Точек |
|---|---|---|---|---|---|---|---|---|
| 11 | варочная панель | 6 | C32 | 30 мА, тип A | ВВГнг(A)-LS 3×6 | 9,8 | 7 | 1 |
| 12 | духовой шкаф | 6 | C16 | 30 мА, тип A | ВВГнг(A)-LS 3×2,5 | 8,9 | 3,5 | 1 |
| 13 | посудомоечная машина | 6 | C16 | 30 мА, тип A | ВВГнг(A)-LS 3×2,5 | 7,3 | 2 | 1 |
| 14 | стиральная машина | 2 | C16 | 30 мА, тип A | ВВГнг(A)-LS 3×2,5 | 13,8 | 2,2 | 1 |
| 15 | розетки ванной комнаты | 2 | C16 | 30 мА, тип A | ВВГнг(A)-LS 3×2,5 | 13,2 | 1,5 | 1 |
| 16 | полотенцесушитель электрический | 2 | C16 | 30 мА, тип A | ВВГнг(A)-LS 3×2,5 | 15,7 | 0,5 | 1 |
| 17 | тёплый пол ванной комнаты, тёплый пол санузла | 2, 10 | C16 | 30 мА, тип A | ВВГнг(A)-LS 3×2,5 | 24 | 0,25 | 2 |
| 18 | слаботочный щит (роутер, ONT) | 7 | C10 | 30 мА, тип A | ВВГнг(A)-LS 3×1,5 | 6 | 0,15 | 1 |
| 19 | розетки гостиной | 11 | C16 | 30 мА, тип A | ВВГнг(A)-LS 3×2,5 | 25,7 | 1 | 3 |
| | Итого по сечениям ВВГнг(A)-LS (все группы щита), м: 3×1,5 — 307,4; 3×2,5 — 303,9; 3×6 — 9,8 | | | | | 621,1 | | |

## Примечания

1. Лист — продолжение однолинейной схемы щита ЩК: начало, данные щитка и условные обозначения — лист 41. Ввод, учёт, вводной аппарат, УЗИП, шины N и PE и ГЗШ показаны там же; шина L листа — та же шина щита.
2. Схема однолинейная: одна линия — фаза, N и PE группы; аппараты — в отключённом положении (ГОСТ 2.702, ГОСТ 2.755). Номера групп — как у точек на планах (гр.). За отметку 0,000 принят уровень чистого пола; высота щита — по плану розеток.
3. Розеточные и мокрые линии — через УЗО или дифавтомат с током утечки не более 30 мА (ПУЭ 7.1.79); в санузле выполнить ДСУП (ПУЭ 7.1.87–7.1.88).
4. УЗО тип A — для линий с электроникой, стиральной и посудомоечной машиной, LED-драйверами; тип AC — только для чисто активной нагрузки.
5. Кабель — медный, исполнение нг(A)-LS (ГОСТ 31565-2012); скрытая прокладка только горизонтально и вертикально, фактические трассы зафиксировать исполнительной схемой до закрытия отделкой.
6. Номинал автомата — не выше допустимого тока кабеля: 1,5 мм² — до 10 А, 2,5 мм² — до 16 А. Резерв щита — не менее 20 % модулей.
7. Расчёт нагрузок, токов КЗ, селективности и сечений — по проекту ЭОМ организации с допуском СРО; лист задаёт состав, расположение и группы.
8. До подключения нагрузки — приёмо-сдаточные испытания с протоколом: сопротивление изоляции линий не менее 0,5 МОм, срабатывание УЗО по току и времени, непрерывность защитных проводников PE (ПУЭ, гл. 1.8).

| | | | | | |
|---|---|---|---|---|---|
| | | | | | Проект: Четырёхкомнатная квартира |
| | Лист | № док. | Подпись | Дата | |
| Дизайнер | Кырлан А.С. | | | 04.11.26 | Однолинейная схема щита (продолжение) |
| | | | | | Стадия: П; Лист: 42; Листов: 120 |

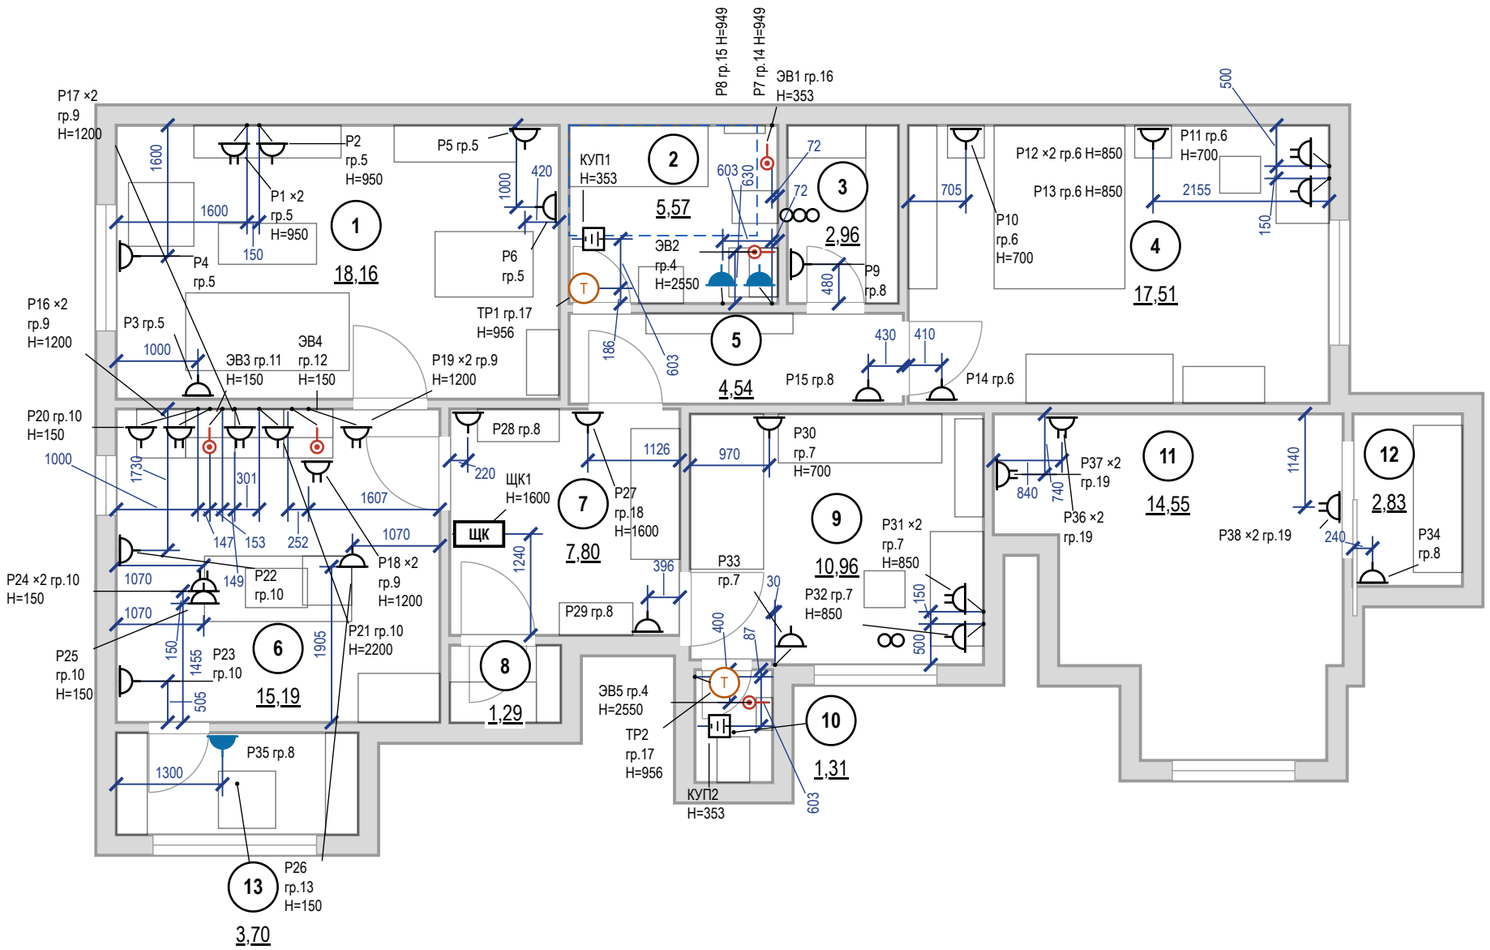


## Условные обозначения

| Знак | Тип изделия | Н, мм | Кол., шт |
|---|---|---|---|
| | Розетка с заземлением | 300 | 13 |
| | То же | у знака | 11 |
| | Блок розеток с заземлением, рамка 2 поста | 300 | 3 |
| | То же | у знака | 8 |
| | Розетка с заземлением IP44 | 300 | 1 |
| | То же | у знака | 2 |
| | Вывод кабеля к прибору | у знака | 5 |
| КУП | КУП (уравнивание потенциалов) | 353 | 2 |
| Т | Терморегулятор тёплого пола | 956 | 2 |
| ЩК | Щит квартирный | 1600 | 1 |

розетка с заземляющим контактом; у знака — марка, ×N — постов в рамке, гр. — группа щита, Н — высота оси, мм

знак разведён для читаемости: точка на стене — у выноски, привязка — до неё

граница зоны 2 ванной (600 мм от ванны/поддона)

мебель и сантехприборы — подложка

стояк: К1 — канализация, В1 — ХВС, Т3 — ГВС

1 — номер помещения, площадь м²


**Итого розеток (механизмов) — 49 шт; рамок — 38 шт: на 1 пост — 27, на 2 поста — 11.**

## Примечания

1. За отметку 0,000 принят уровень чистого пола. Высоты Н — от чистого пола до оси изделия; привязки — от чистовой грани стены до оси механизма (у рамки на несколько постов — до оси рамки).
2. Розетки без отметки Н у знака — на высоте 300 мм от чистого пола до оси механизма; выводы кабеля — по паспорту прибора.
3. Розетки в санузле — только вне зон 0–2 (ПУЭ 7.1.48, ГОСТ Р 50571.7.701-2024), IP44, через УЗО 30 мА.
4. Розеточные и мокрые линии — через УЗО или дифавтомат с током утечки не более 30 мА (ПУЭ 7.1.79); в санузле выполнить ДСУП (ПУЭ 7.1.87–7.1.88).
5. Кабель — медный, исполнение нг(А)-LS (ГОСТ 31565-2012); скрытая прокладка только горизонтально и вертикально, фактические трассы зафиксировать исполнительной схемой до закрытия отделкой.
6. Расчёт нагрузок, токов КЗ, селективности и сечений — по проекту ЭОМ организации с допуском СРО; лист задаёт состав, расположение и группы.

| | | | | | |
|---|---|---|---|---|---|
| | | | | | Проект: Четырёхкомнатная квартира — М 1:75 |
| | Лист | № док. | Подпись | Дата | |
| Дизайнер | Кырлан А.С. | | | 04.11.26 | План розеток и электровыводов |

| Стадия | Лист | Листов |
|---|---|---|
| П | 43 | 120 |

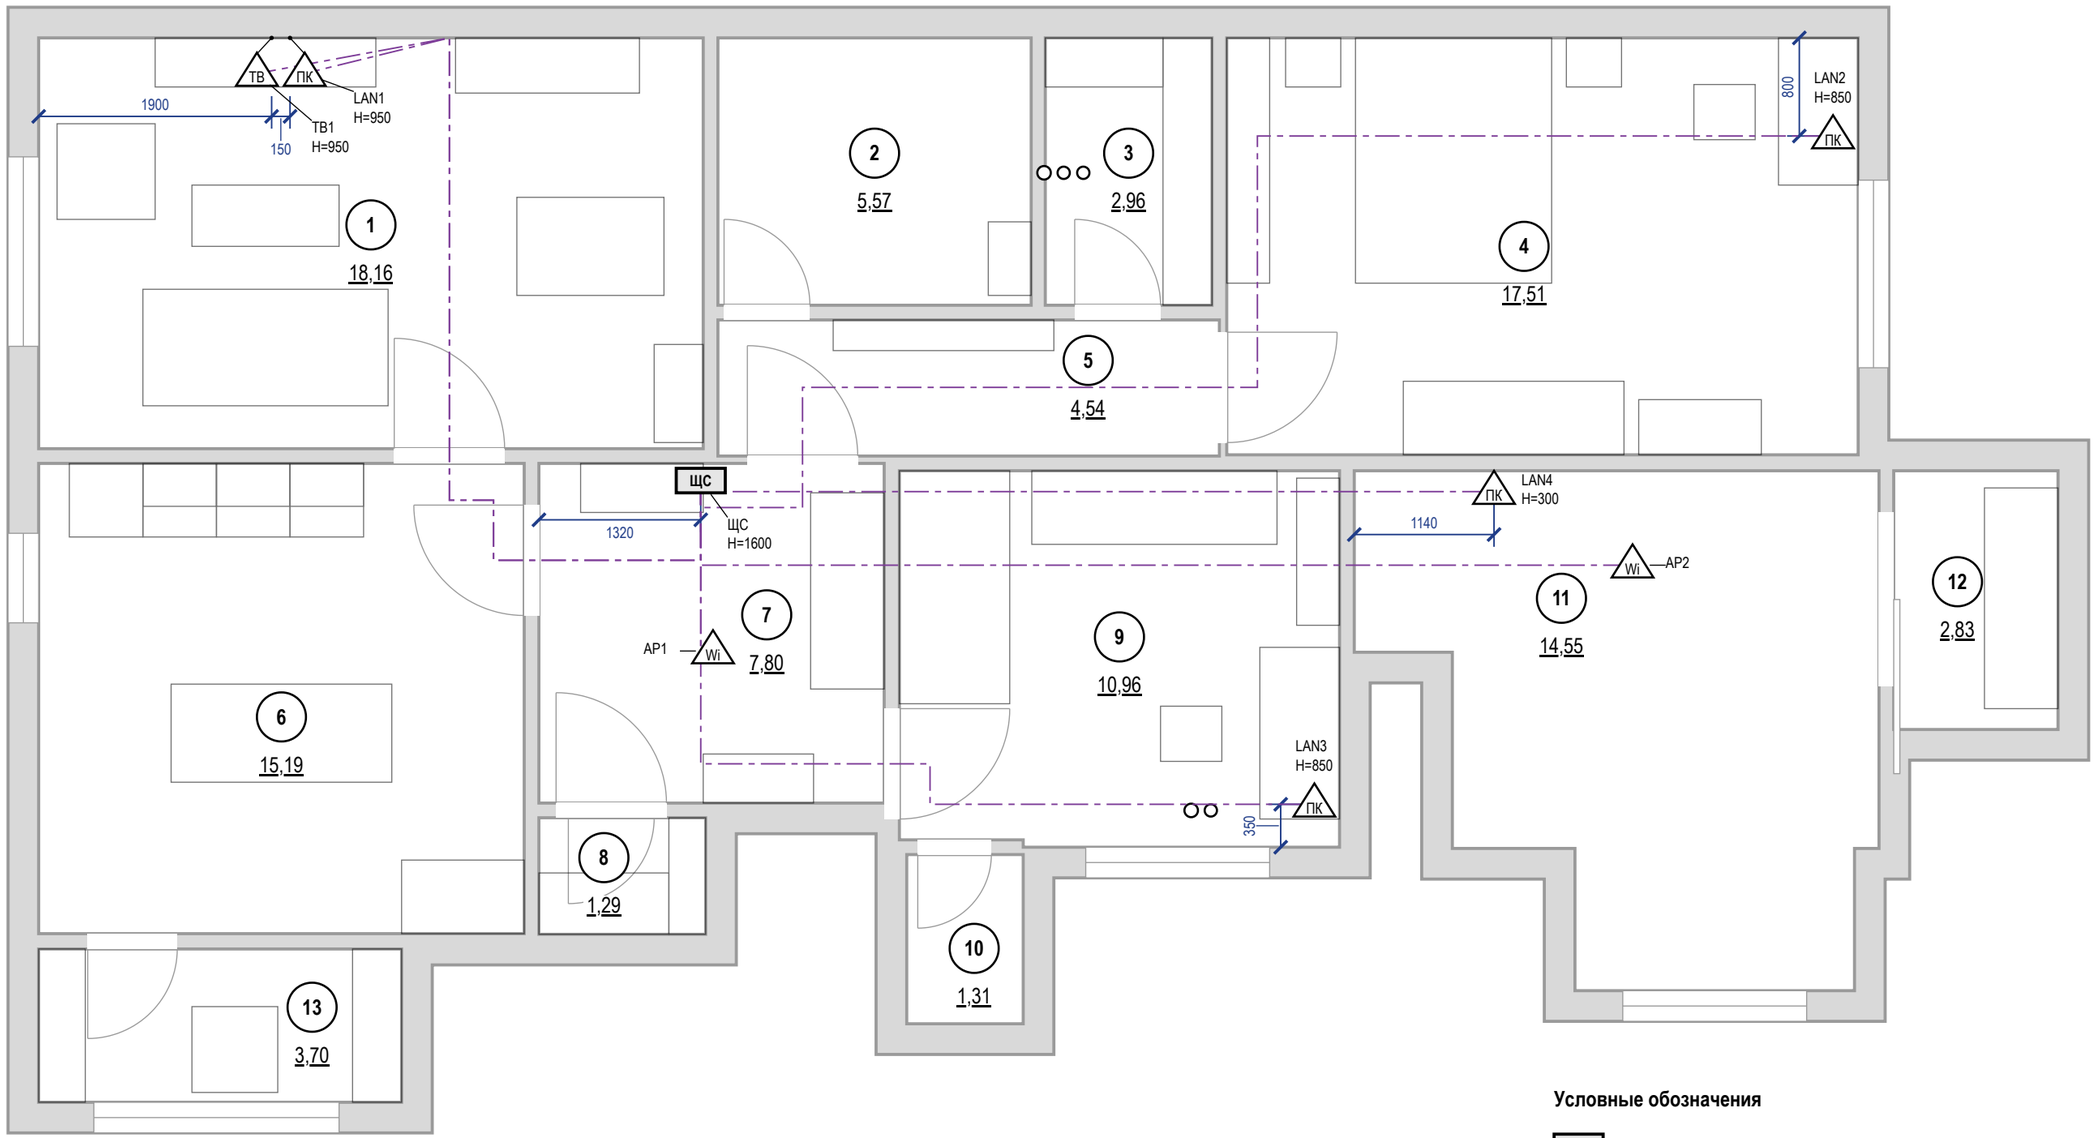


## Условные обозначения

| | |
|---|---|
| ЩС | щит слаботочный: ввод провайдера, роутер, коммутатор |
| ПК | розетка компьютерная RJ45 |
| ТВ | розетка телевизионная |
| Wi | точка доступа Wi-Fi (питание PoE) |
| — — — | кабель от ЩС до точки, отдельным лучом |
| ▭ | мебель и сантехприборы — подложка |
| ○ | стояк: К1 — канализация, В1 — ХВС, Т3 — ГВС |
| 1 | номер помещения, площадь м² |


## Примечания

1. За отметку 0,000 принят уровень чистого пола. Высоты Н — от чистого пола до оси изделия; привязки — от чистовой грани стены до оси механизма (у рамки на несколько постов — до оси рамки).
2. Высота установки, не указанная на плане: розетки LAN и ТВ — 300 мм от чистого пола.
3. Слаботочные кабели — отдельно от силовых: в своей трубе или лотке, при параллельной прокладке не ближе 100 мм к силовым, пересечения под прямым углом; каждую точку — отдельным кабелем от ЩС без скруток.
4. Трассы на листе — принципиальные; фактические зафиксировать исполнительной схемой до закрытия отделкой. Силовые линии, УЗО 30 мА, ДСУП, кабель нг(А)-LS — по листам розеток и щита.
5. Проект силовой части и расчёт токов КЗ — по проекту ЭОМ; слаботочная часть согласуется с провайдером и управляющей компанией (домофон, коллективное ТВ).

| | | | | | |
|---|---|---|---|---|---|
| | | | | | Проект: Четырёхкомнатная квартира — М 1:50 |
| | Лист | № док. | Подпись | Дата | План слаботочных сетей |
| Дизайнер | Кырлан А.С. | | | 04.11.26 | Стадия: П; Лист: 44; Листов: 120 |

## Условные обозначения

- светильник встраиваемый точечный
- Св1·L1 — марка светильника (как в ведомости и на развёртках) · группа включения L (лист 47)
- мебель и сантехприборы — подложка
- светильник подвесной
- Д — извещатель пожарный дымовой автономный
- стояк: К1 — канализация, В1 — ХВС, Т3 — ГВС
- светильник настенный (бра), Н — высота оси
- Т° — извещатель пожарный тепловой
- 1 — номер помещения, площадь м²
- светодиодная лента в профиле / в карнизе короба
- БП — блок питания LED, с доступом (люк от 100×100 мм)

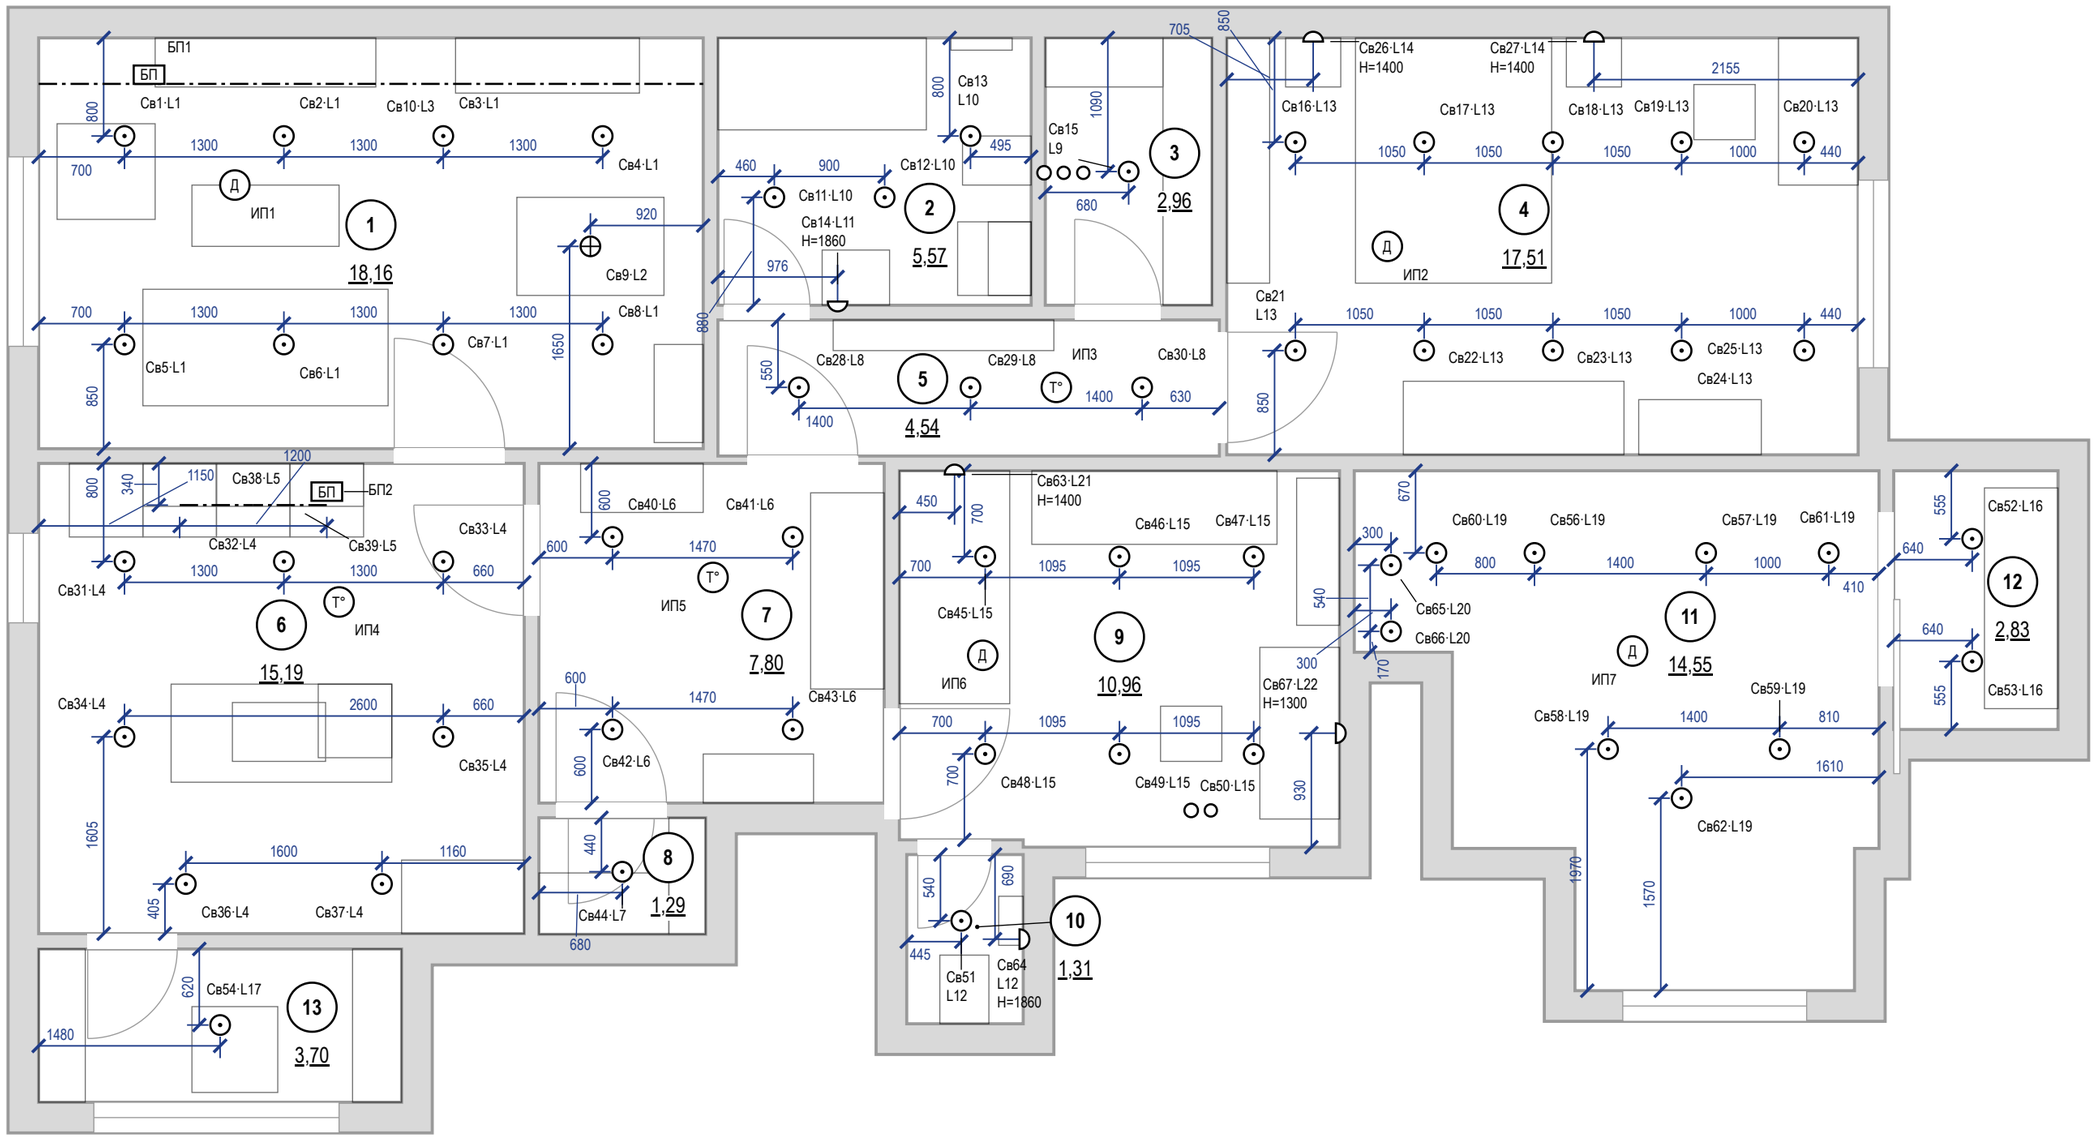


## Примечания

1. За отметку 0,000 принят уровень чистого пола. Высоты Н — от чистого пола до оси изделия; привязки — от чистовой грани стены до оси механизма (у рамки на несколько постов — до оси рамки).
2. Высота установки, не указанная на плане: светильники — на потолке; настенные — по отметке Н у знака. Привязки — до оси светильника от чистовой грани стены, по рядам.
3. Во влажных помещениях — светильники не ниже IP44; в зонах 0–2 ванной — по ГОСТ Р 50571.7.701-2024 (зона 1 — IPX5).
4. LED-лента в карнизе подсветки короба — по линии карниза с плана потолков; блок питания — в люке короба (БП на плане), питание ленты длиннее 5 м — с двух концов.
5. Розеточные и мокрые линии — через УЗО или дифавтомат с током утечки не более 30 мА (ПУЭ 7.1.79); в санузле выполнить ДСУП (ПУЭ 7.1.87–7.1.88).
6. Кабель — медный, исполнение нг(А)-LS (ГОСТ 31565-2012); скрытая прокладка только горизонтально и вертикально, фактические трассы зафиксировать исполнительной схемой до закрытия отделкой.
7. Расчёт нагрузок, токов КЗ, селективности и сечений — по проекту ЭОМ организации с допуском СРО; лист задаёт состав, расположение и группы.
8. Ведомость светильников (тип, количество, мощность, поток, Tц, Ra) — лист 46.

| | | | | | |
|---|---|---|---|---|---|
| | | | | | Проект: Четырёхкомнатная квартира — М 1:50 |
| | Лист | № док. | Подпись | Дата | |
| Дизайнер | Кырлан А.С. | | | 04.11.26 | План освещения |
| | | | | | Стадия: П; Лист: 45; Листов: 120 |

## Параметры светильников для подбора

| Поз. | Марки | Наименование | Установка | Кол. | P, Вт | Σ P, Вт | Ф, лм | Тц, К | Ra | Угол, ° | IP | Дим. | Слой | Группа | Пом. |
|---|---|---|---|---|---|---|---|---|---|---|---|---|---|---|---|
| 1 | Св1–Св8, Св16–Св19, Св20, Св21–Св24, Св25, Св31–Св37, Св56–Св62 | Встраиваемый точечный | в ГКЛ, корпус ≤ 70 мм | 32 | 12 | 384 | 1000 | 3000 | 90 | — | 20 | — | общий | L1, L4, L13, L19 | 1, 4, 6, 11 |
| 2 | Св9 | Подвесной | подвес, низ H=1600 | 1 | 15 | 15 | 1200 | 2700 | 90 | — | 20 | — | рабочий | L2 | 1 |
| 3 | Св10 | Лента светодиодная 24 В | в карнизе короба, профиль с рассеивателем | 5,4 м | 9,6/м | 52 | 900/м | 2700 | 90 | — | 20 | да | акцентный | L3 | 1 |
| 4 | Св11, Св12, Св13, Св51 | Встраиваемый точечный | в ГКЛ, корпус ≤ 70 мм | 4 | 6 | 24 | 500 | 3000 | 90 | — | 44 | — | общий | L10, L12 | 2, 10 |
| 5 | Св14, Св64 | Светильник над зеркалом, драйвер встроен | над зеркалом, H=1860 | 2 | 8 | 16 | 600 | 3000 | 90 | — | 44 | — | рабочий | L11, L12 | 2, 10 |
| 6 | Св15, Св40–Св44, Св52, Св53, Св65, Св66 | Встраиваемый точечный | в ГКЛ, корпус ≤ 70 мм | 10 | 6 | 60 | 500 | 3000 | 90 | — | 20 | — | общий, акцентный | L6, L7, L9, L16, L20 | 3, 7, 8, 11, 12 |
| 7 | Св26, Св27, Св63 | Настенный (бра) | на стене, H=1400 | 3 | 6 | 18 | 400 | 2700 | 90 | 60 | 20 | — | рабочий | L14, L21 | 4, 9 |
| 8 | Св28–Св30 | Встраиваемый точечный | в ГКЛ, корпус ≤ 70 мм | 3 | 5 | 15 | 400 | 3000 | 90 | — | 20 | — | общий | L8 | 5 |
| 9 | Св38, Св39 | Линейный светильник | на поверхности | 1,2 м | 8 | 16 | 700 | 3000 | 90 | — | 20 | — | рабочий | L5 | 6 |
| 10 | Св45–Св50 | Встраиваемый точечный | в ГКЛ, корпус ≤ 70 мм | 6 | 13 | 78 | 1100 | 3000 | 90 | — | 20 | — | общий | L15 | 9 |
| 11 | Св67 | Бра подсветки рабочего места, стол M_35 | на стене, H=1300 | 1 | 7 | 7 | 450 | 3000 | 90 | 60 | 20 | — | рабочий | L22 | 9 |
| 12 | Св54 | Встраиваемый точечный | в ГКЛ, корпус ≤ 70 мм | 1 | 9 | 9 | 800 | 3000 | 90 | — | 44 | — | общий | L17 | 13 |
| | | **Итого** | | **63 шт + 6,6 м** | | **694** | | | | | | | | | |

## LED-ленты, линейные светильники и блоки питания

| Марка | Пом. | L, м | U, В | Вт/м | Σ P, Вт | БП | P БП, Вт | Загр., % | Питание | Доступ к БП |
|---|---|---|---|---|---|---|---|---|---|---|
| Св10 | 1 | 5,4 | 24 | 9,6 | 52 | БП1 | 100 | 52 | с одного конца | люк 300×300 в коробе потолка у стены A |
| Св38 | 6 | 0,6 | 24 | — | 8 | БП2 | 30 | 53 | встроенный ввод | в навесном модуле M_25, съёмная панель |
| Св39 | 6 | 0,6 | 24 | — | 8 | БП2 | 30 | 53 | встроенный ввод | в навесном модуле M_25, съёмная панель |

## Сценарии (помещения со светорегуляторами)

| Помещение | Сценарий | Горят группы (уровень) | Управление |
|---|---|---|---|
| 1. Зал | Вечер | L2 подвес над обеденным столом — вкл.;<br>L3 лента в карнизе (диммер) — 50 %; остальные выкл. | светорегулятор S2;<br>выключатель S1 |
| | Гости | L1 общий свет (споты) — вкл.;<br>L2 подвес над обеденным столом — вкл.;<br>L3 лента в карнизе (диммер) — 100 % | светорегулятор S2;<br>выключатель S1 |
| | Кино | L3 лента в карнизе (диммер) — 20 %; остальные выкл. | светорегулятор S2 |
| | Уборка | L1 общий свет (споты) — вкл.;<br>L2 подвес над обеденным столом — вкл.; остальные выкл. | выключатель S1 |

## Примечания


1. Позиции и марки Св — те же, что на плане освещения (лист 45); группы L — по плану выключателей (лист 47).
2. Модели светильников не выбраны: лист — техническое задание на подбор. Модель по строке таблицы: поток, Тц, Ra, угол, IP и регулировка яркости не хуже указанных, мощность не больше; встраиваемые — под глубину короба (графа «Установка»). IP 20 — сухие помещения. После выбора моделей (артикул, производитель) лист выпускается как «Спецификация светильников».
3. Длина LED-ленты в карнизе — по линии карниза плана потолков (лист 36); Σ P = Вт/м × длина. Блок питания загружен не больше чем на 80 %; лента 24 В длиннее 10 м питается с двух концов; доступ к блоку питания — люк ревизии 300×300 мм или место, указанное в таблице.
4. Сценарии: % — яркость группы на светорегуляторе; «вкл.» — группа на обычной клавише; группы, не названные в строке, выключены. Светильники и блоки питания групп на светорегуляторе — с регулировкой яркости. Клавиши и светорегуляторы — лист 47.
5. Мощность и поток в таблице — требования к подбору (поток не меньше, мощность не больше указанных); после выбора модели — по её паспорту, Σ P — установленная мощность освещения. Оценка освещённости — на плане освещения; это не светотехнический расчёт.

| | | | | | |
|---|---|---|---|---|---|
| | | | | | Проект: Четырёхкомнатная квартира |
| | Лист | № док. | Подпись | Дата | |
| Дизайнер | Кырлан А.С. | | | 04.11.26 | Техническое задание на подбор светильников |

| Стадия | Лист | Листов |
|---|---|---|
| П | 46 | 120 |

**Условные обозначения**

- ⊕ — светильник подвесной
- L1 — группа включения у светильника
- светильник настенный (бра), H — высота оси
- стояк: К1 — канализация, В1 — ХВС, Т3 — ГВС
- светодиодная лента в профиле / в карнизе короба
- (1) — номер помещения, площадь м²

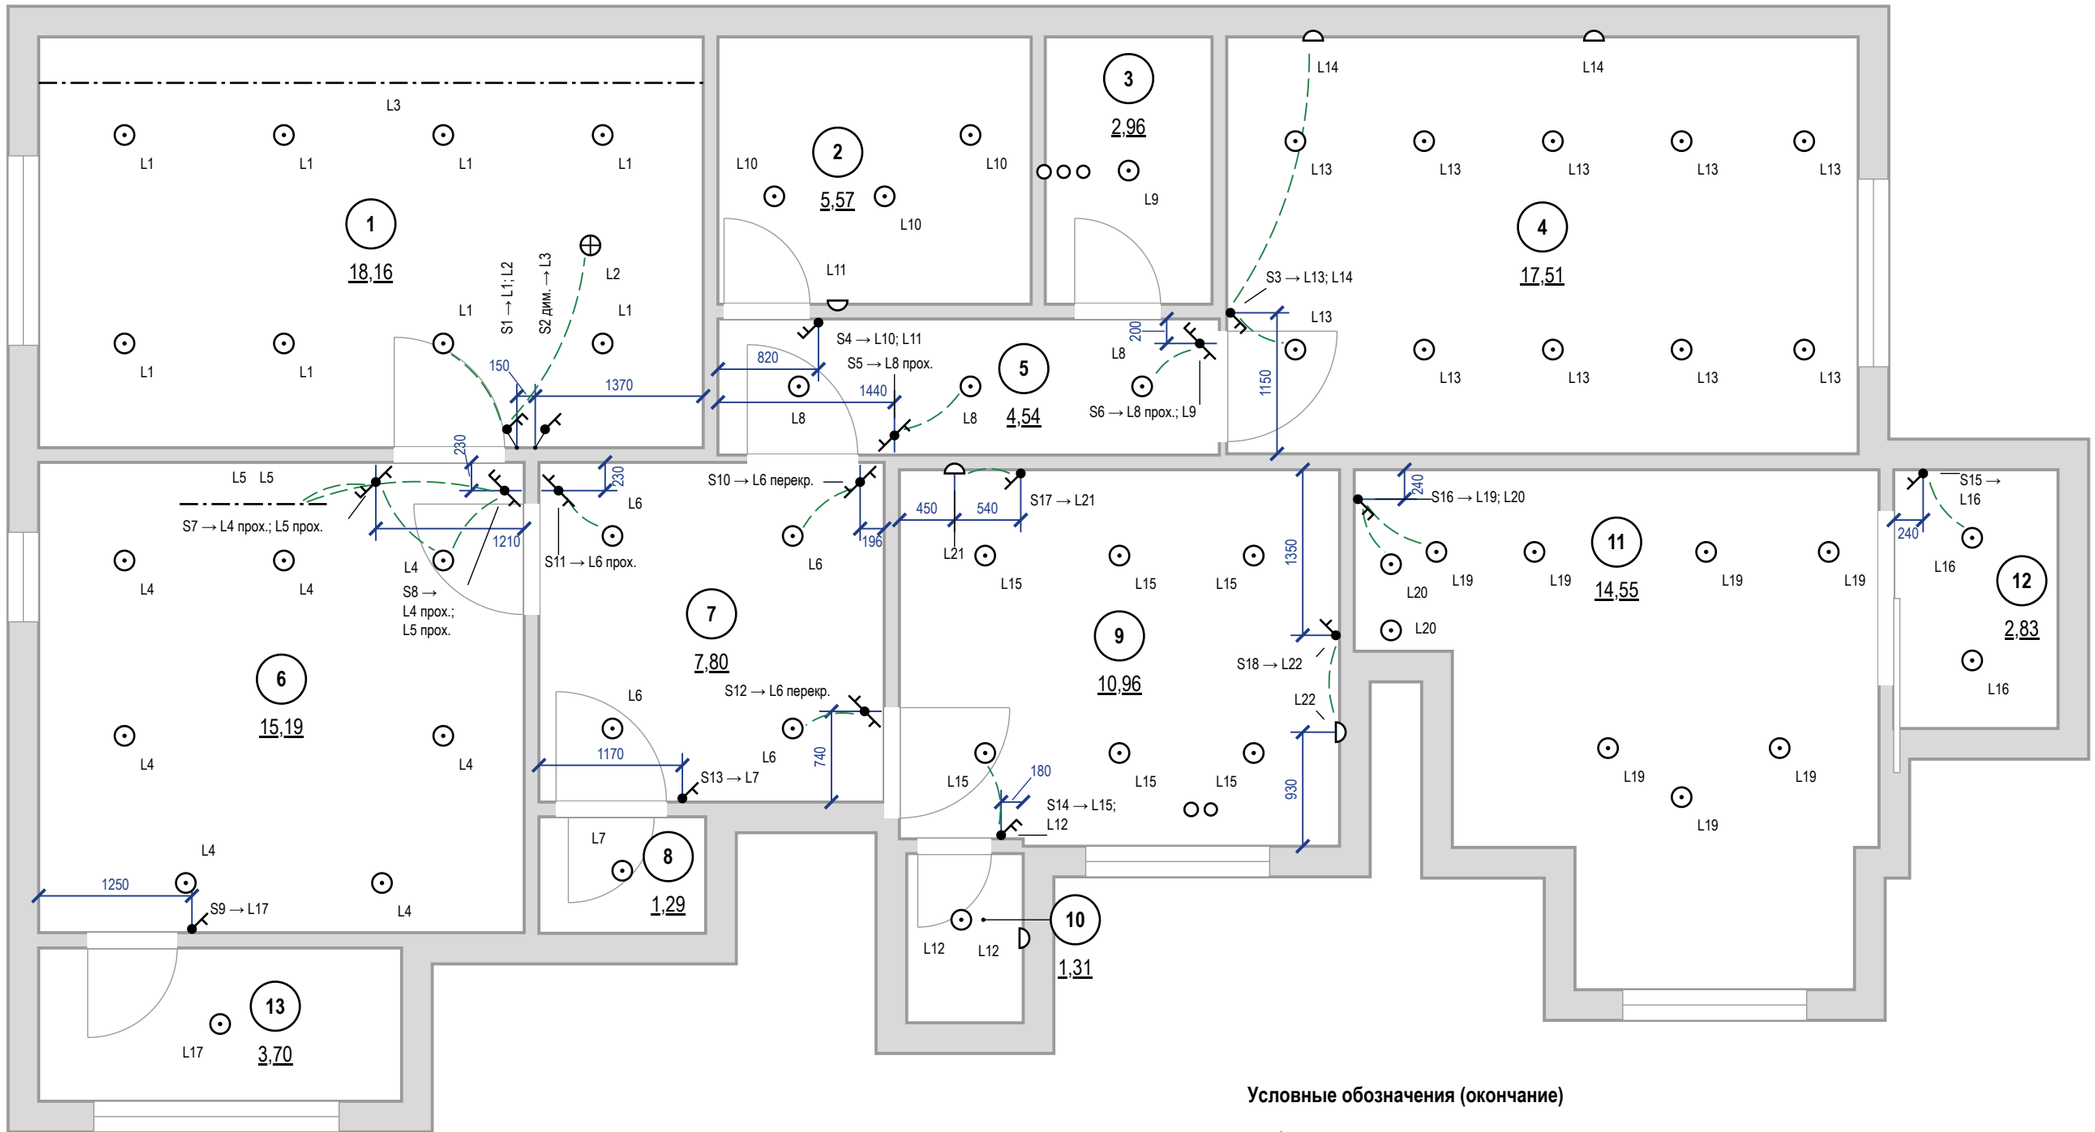



## Примечания

1. За отметку 0,000 принят уровень чистого пола. Высоты H — от чистого пола до оси изделия; привязки — от чистовой грани стены до оси механизма (у рамки на несколько постов — до оси рамки).
2. Высота установки, не указанная на плане: выключатели — 900 мм от чистого пола (у кровати и другие — H у марки), со стороны дверной ручки (ПУЭ 7.1.51).
3. Какой выключатель какие светильники включает — по номеру группы L: у выключателя (S1 → L1; L2 — клавиши по порядку) и у каждого светильника. Пунктир подсказка к ближайшему светильнику группы в том же помещении (не дальше 3 м), это не трасса кабеля; выключатель за стеной (у двери санузла) и далёкая группа — только номер группы.
4. Группы из нескольких мест (L8 — S5, S6; L4 — S7, S8; L5 — S7, S8; L6 — S10, S11, S12): на крайних местах — проходные клавиши, на промежуточных перекрёстные; механизмы — в ведомости изделий.
5. Светорегулятор — по заднему фронту (для LED-драйверов), совместимость с драйверами проверить до закупки.
6. Розеточные и мокрые линии — через УЗО или дифавтомат с током утечки не более 30 мА (ПУЭ 7.1.79); в санузле выполнить ДСУП (ПУЭ 7.1.87–7.1.88).
7. Кабель — медный, исполнение нг(А)-LS (ГОСТ 31565-2012); скрытая прокладка только горизонтально и вертикально, фактические трассы зафиксировать исполнительной схемой до закрытия отделкой.
8. Расчёт нагрузок, токов КЗ, селективности и сечений — по проекту ЭОМ организации с допуском СРО; лист задаёт состав, расположение и группы.

## Условные обозначения (окончание)

- выключатель одноклавишный
- выключатель двухклавишный (флажков — по числу клавиш)
- выключатель с проходной или перекрёстной клавишей (обратный флажок); тип клавиши — в подписи
- S1 → — марка → группы по клавишам (через «;»): прох. проходной, перекр. — перекрёстный, дим. светорегулятор; H — высота
- связь: выключатель → ближайший светильник группы в том же помещении (не трасса кабеля); полный состав группы по номеру L
- светильник встраиваемый точечный

| | | | | | |
|---|---|---|---|---|---|
| | | | | | Проект: Четырёхкомнатная квартира — М 1:50 |
| | Лист | № док. | Подпись | Дата | Управление светильниками — Стадия: П; Лист: 47; Листов: 120 |
| Дизайнер | Кырлан А.С. | | | 04.11.26 | |

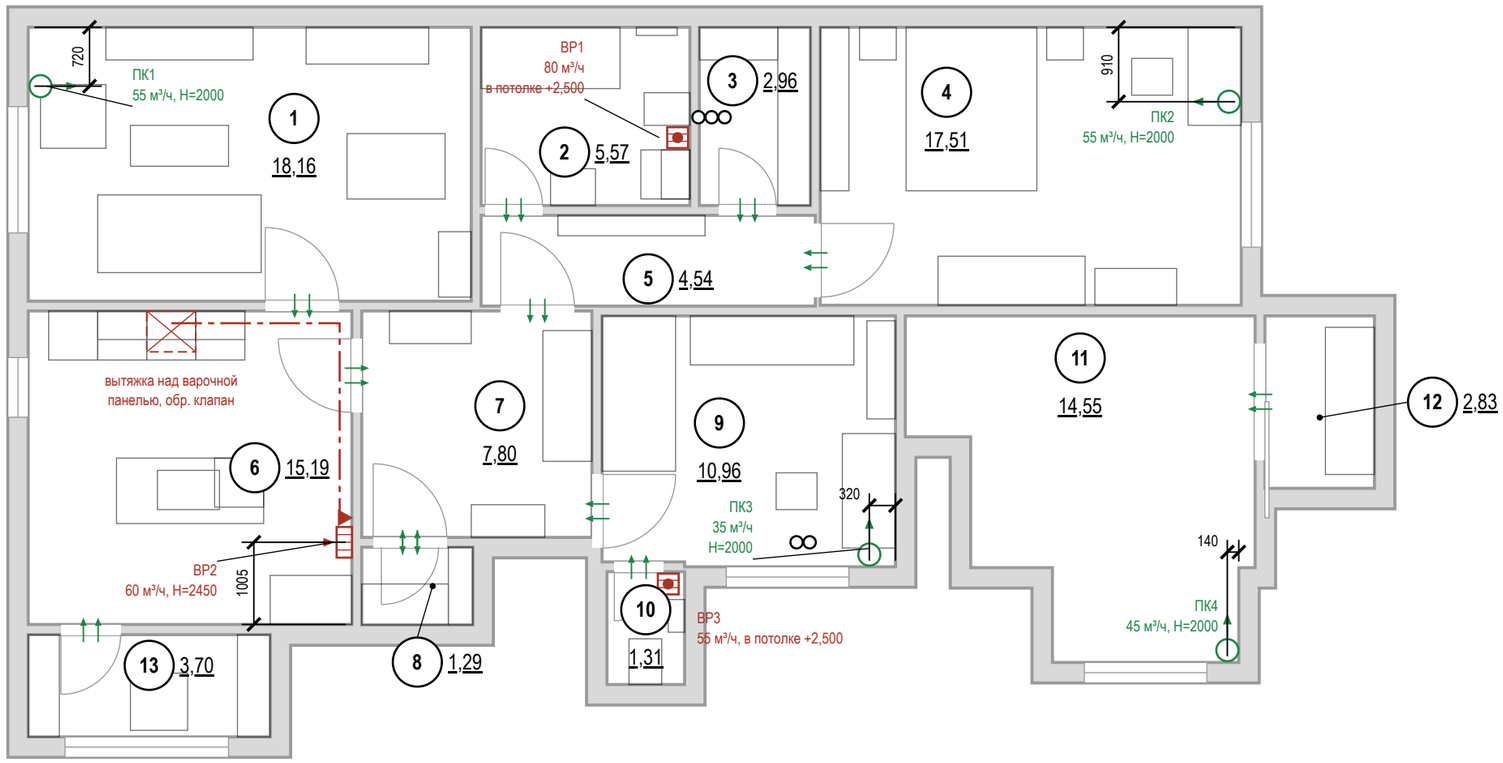


## Условные обозначения

- стояк: К1 — канализация, В1 — ХВС, Т3 — ГВС
- номер помещения, площадь м²
- вытяжная решётка в вентканал: марка, расход м³/ч, Н центра от чистого пола
- вентилятор с обратным клапаном в подшивном потолке, воздуховод за потолком до канала
- приточный клапан (КИВ) в наружной стене: марка, расход, Н центра
- переток: зазор под полотном или переточная решётка
- кухонная вытяжка над варочной панелью
- воздуховод кухонной вытяжки в коробе под потолком
- отдельный вход воздуховода в вентканал, обратный клапан

## Воздухообмен, м³/ч

| № | Помещение | Выт. норма | Выт. проект | Прит. норма | Прит. проект | Устрой-ства |
|---|---|---|---|---|---|---|
| 1 | Зал | | | 55 | 55 | ПК1 |
| 2 | Ванная комната | 50 | 80 | | | ВР1 |
| 3 | Тёмная комната | 2 | | | | переток |
| 4 | Детская 1 | | | 53 | 55 | ПК2 |
| 6 | Кухня | 60 | 60 | | | ВР2 |
| 8 | Гардеробная 2 | 1 | | | | переток |
| 9 | Детская 2 | | | 33 | 35 | ПК3 |
| 10 | Санузел | 25 | 55 | | | ВР3 |
| 11 | Гостиная | | | 44 | 45 | ПК4 |
| 12 | Гардеробная 1 | 2 | | | | переток |
| | **Итого** | **140** | **195** | **185** | **190** | |

Воздухообмен квартиры — по большей из сумм притока и вытяжки: норма 185 м³/ч, проект 195 м³/ч.
Вытяжка не меньше притока — баланс сведён.

**Привязки — до обмера**
Вентканалы в исходных данных не заданы: решётки и вход вытяжки показаны у стояков К1 (вентблок у мокрой зоны). До черновых работ — обмер каналов и проверка тяги; лист перевыпустить по факту.

## Примечания


1. Расчёт систем ОВ и подбор оборудования — проектная организация с допуском СРО; лист даёт места, трассы и привязки.
2. Нормы вытяжки — СП 54.13330.2022 (Изм. 1, 2), табл. 7.1: кухня с электроплитой 60 м³/ч, с газовой 100; ванная и совмещённый санузел 50; уборная 25; гардеробная 0,2 ч⁻¹. Приток в жилые — 3 м³/ч на 1 м² (менее 20 м² общей площади на человека), иначе 30 м³/ч на человека.
3. Вентканалы и шахты не сужать, не переносить и не закрывать; вентилятор и кухонная вытяжка — через обратный клапан, без перекрытия естественной тяги.
4. Проектные расходы — не ниже нормы, вытяжка сведена с притоком вентиляторами мокрых помещений. Клапаны — в простенке у окна, центр 2000 мм, не над кроватью, не ближе 300 мм к стоякам отопления; типоразмер — на расход.
5. Под подшивным потолком вытяжка — в потолке, воздуховодом за потолком до канала. Кухонная вытяжка в воздухообмен не включена: воздуховод не менее Ø125 в коробе, вход в канал отдельный.
6. Переток — зазор под полотнами межкомнатных дверей или переточная решётка.
7. Кондиционирование заданием не предусмотрено; при установке трассы фреона и дренажа (не менее 40 мм/м, в К1 через сифон) и питание заложить до черновых работ.
8. Привязки оборудования — по паспортам приобретённых моделей, до черновых работ.

| | | | | | |
|---|---|---|---|---|---|
| | | | | | Проект: Четырёхкомнатная квартира — **М 1:75** |
| | Лист | № док. | Подпись | Дата | |
| Дизайнер | Кырлан А.С. | | | 04.11.26 | План вентиляции |

| Стадия | Лист | Листов |
|---|---|---|
| П | 48 | 120 |

## Условные обозначения

- (1) — номер помещения, площадь м²
- радиатор отопления (марка РО-N, длина по плану)
- (Т) — клапан с термоголовкой на подаче
- стояк отопления, подающий (Ст Т1-N)
- стояк отопления, обратный (Ст Т2-N)
- Т1 — отопление, подающий трубопровод
- Т2 — отопление, обратный трубопровод

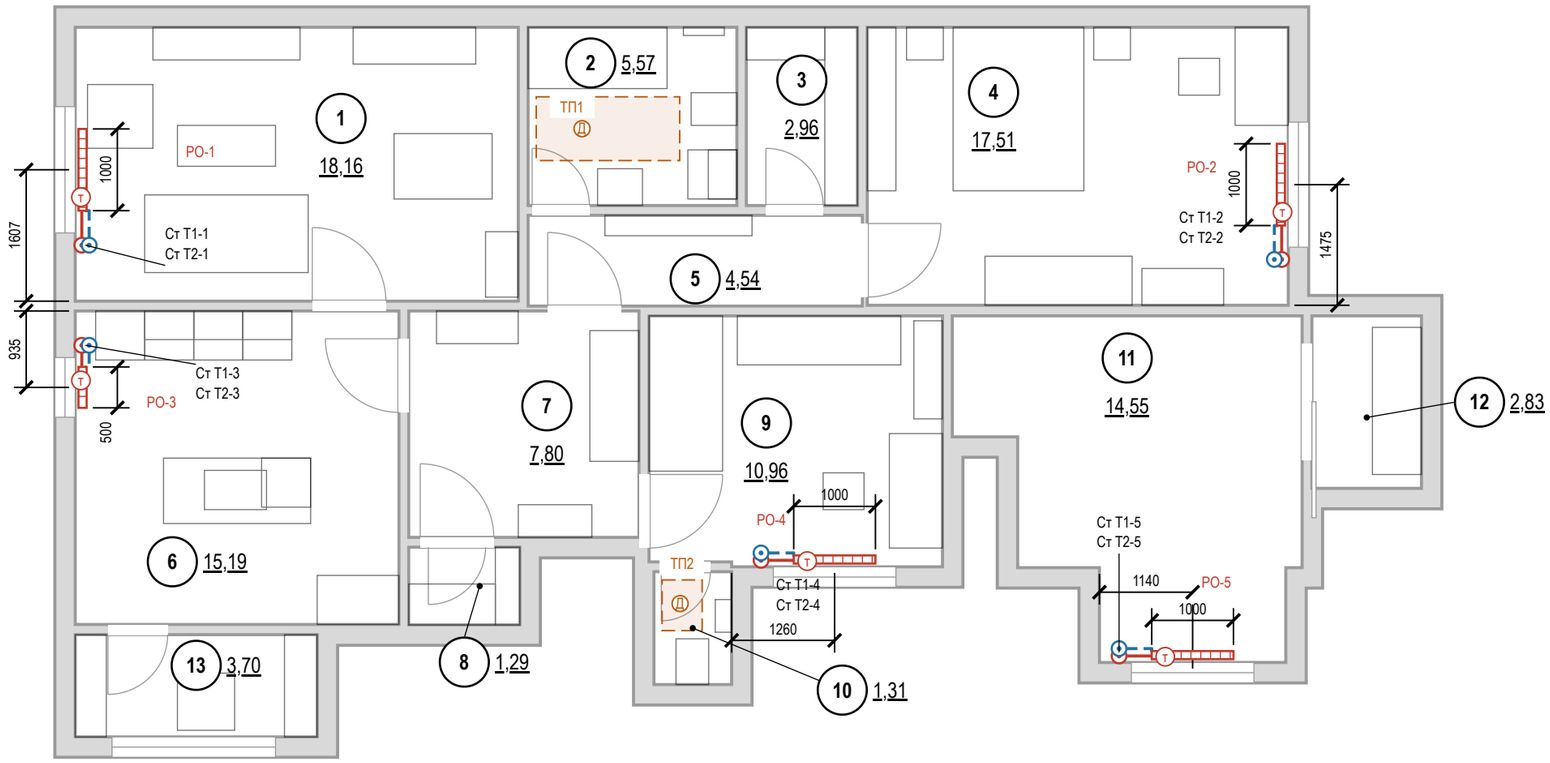


## Ведомость радиаторов

| Марка | Помещение | Тип | Д×В×Г, мм | Низ / стена | Q, Вт |
|---|---|---|---|---|---|
| РО-1 | 1. Зал | панельный | 1000×500×100 | 120 / 40 | расч. |
| РО-2 | 4. Детская 1 | панельный | 1000×500×100 | 120 / 40 | расч. |
| РО-3 | 6. Кухня | панельный | 500×500×100 | 120 / 40 | расч. |
| РО-4 | 9. Детская 2 | панельный | 1000×500×100 | 120 / 40 | расч. |
| РО-5 | 11. Гостиная | панельный | 1000×600×100 | 120 / 40 | расч. |

тип и мощность — по теплотехническому расчёту
Низ — от чистого пола, стена — зазор до задней панели, мм.

**Привязки — до обмера**
Стояки отопления в исходных данных не заданы: показаны у откосов окон, подводки — принципиально. До черновых работ — обмер стояков и паспорта приборов; лист перевыпустить по факту.

## Примечания

1. Расчёт системы отопления, теплопотерь и подбор приборов — проектная организация с допуском СРО; лист даёт места и привязки.
2. Электрический тёплый пол: ТП1 — пом. 2, мат 1755×780 мм, 205 Вт; ТП2 — пом. 10, мат 490×620 мм, 50 Вт; контуры показаны пунктиром; датчик температуры (Д) — в гофротрубе, трасса к терморегулятору — по обмеру. Марка мата и точное положение датчика — при закупке и по обмеру.
3. Тип, длина и мощность радиаторов — по теплотехническому расчёту; лист задаёт места, зазоры и подключение.
4. Радиаторы — под каждым окном жилых комнат и кухни, центр по оси проёма, длина 0,7 ширины окна (кратно 100); окончательно — по расчёту.
5. Зазоры радиатора: низ не менее 100 мм от чистого пола, верх не менее 100 мм до подоконника, 30–50 мм от стены до задней панели; центр по оси окна с допуском ±20 мм. Верх до подоконника — 180 мм.
6. Радиаторы не закрывать глухими коробами и мебелью; перенос и замена приборов в многоквартирном доме — переустройство, согласование с управляющей организацией (ЖК РФ ст. 25–26); вынос на лоджию запрещён.
7. Трубы отопления через межквартирные стены не прокладывать (СП 51.13330.2011, п. 9.19); через перекрытия и перегородки — в гильзах.
8. Привязки приборов и подводок — по паспортам приобретённых радиаторов и клапанов, до черновых работ.
9. До закрытия отделкой трубопроводы отопления испытать гидростатическим давлением с оформлением акта (СП 73.13330.2016, 7.2–7.3).


| | | | | | |
|---|---|---|---|---|---|
| | | | | | Проект: Четырёхкомнатная квартира — **М 1:75** |
| | Лист | № док. | Подпись | Дата | |
| Дизайнер | Кырлан А.С. | | | 04.11.26 | План отопления |
| | | | | | Стадия: П; Лист: 49; Листов: 120 |

## Спецификация плинтусов






| Наименование | Помещения | Длина, м (с запасом) |
|---|---|---|
| Плинтус МДФ под окраску 80×16 мм, крепление к стене, окраска в цвет Tikkurila F497 | 1, 3, 4, 6, 8, 9, 11, 12 | 99 |
| Плинтус МДФ под окраску 80×16 мм, крепление к стене, окраска в цвет Tikkurila J484 | 5, 7 | 19 |
| Плинтус из керамогранита пола, подрезка 80 мм, верхняя кромка с запилом 45°, h = 80 мм, крепление к стене | 13 | 9 |

## Отметки по высоте

| | |
|---|---|
| **±0,000** | чистый пол пом. 1, 3–9, 11, 12; отсчёт высот |
| **−0,015** | чистый пол пом. 2, 10, ниже на 15 мм |
| **−0,030** | чистый пол пом. 13, ниже на 30 мм |
| **−0,170** | верх плиты — расчёт, не замер (задание на обмер) |
| **сущ. пол** | снимается до плиты; не замерен (задание на обмер) |

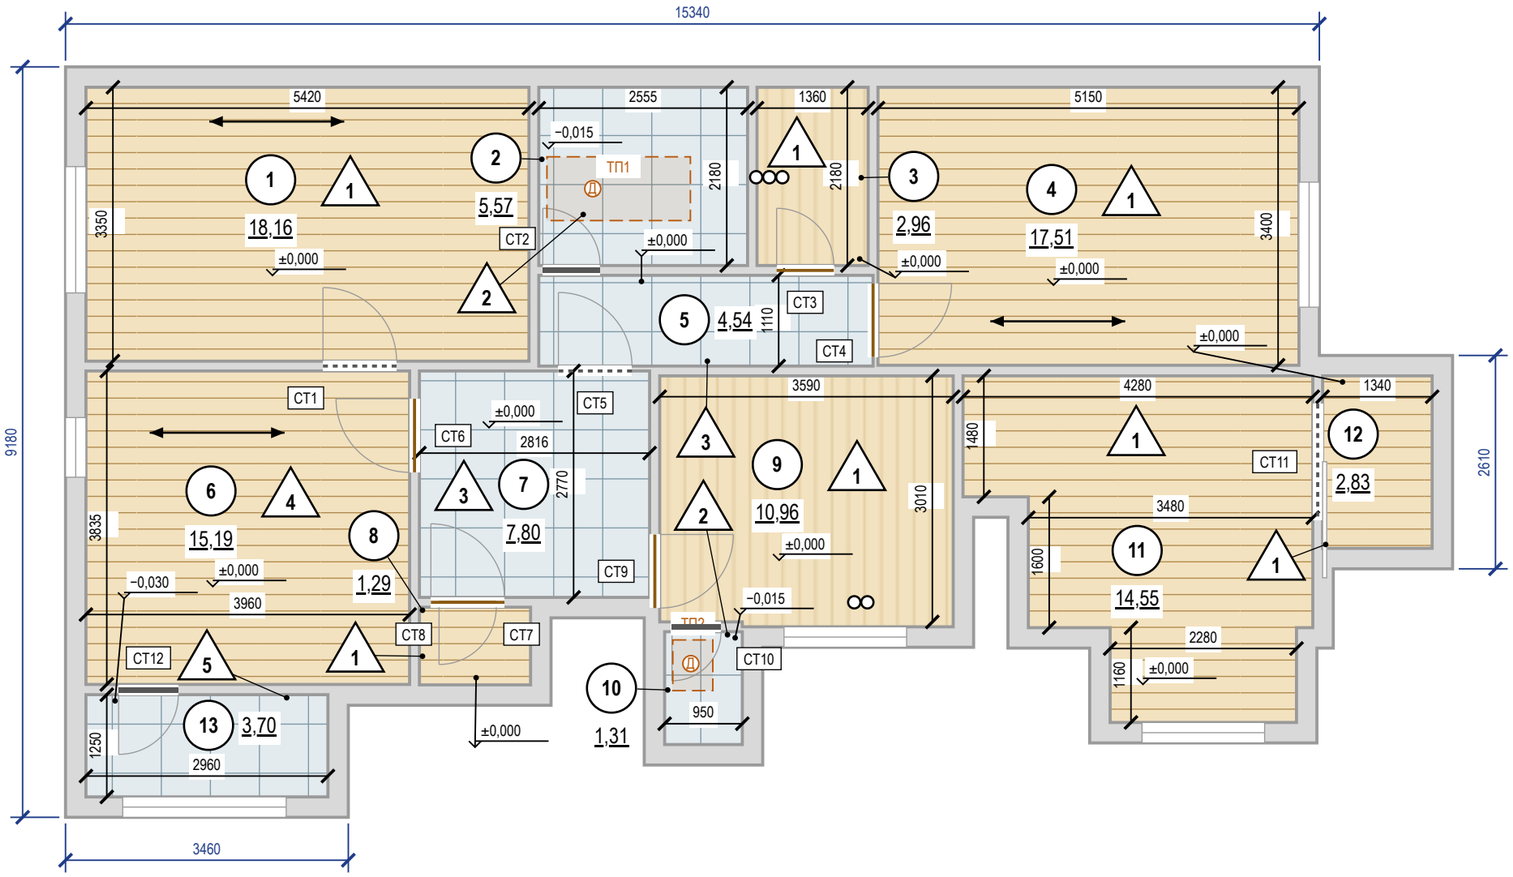


## Экспликация полов

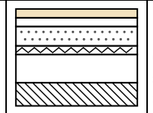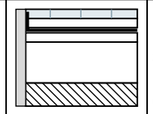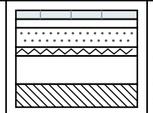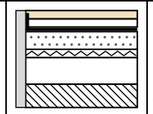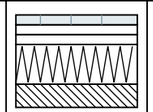
| Номер помещения | Тип пола | Схема пола | Данные элементов пола (наименование, толщина, основание), мм | Площадь, м² |
|---|---|---|---|---|
| 1, 3, 4, 8, 9, 11, 12 | 1 |  | Инженерная доска дуб на клею — 14<br>Клей паркетный МС-полимерный — 1<br>Стяжка ЦПС М300 (В22,5), фибра, по звукоизоляции — 55<br>Звукоизоляция — минплита 110 кг/м³ 20<br>Засыпка керамзитовая фр. 0–5, уплотнённая — 80<br>Плита перекрытия монолитная<br>Всего 170 мм; ЧП ±0,000, верх плиты −0,170 | 68,26 |
| 2, 10 | 2 |  | Керамогранит 600×600×10 — 10<br>Нагревательный мат в слое клея С2 TE S1 — 8<br>Гидроизоляция обмазочная, 2 слоя (заход на стены — по ведомости отделки) — 2<br>Сборное основание ГВЛВ 2×12,5 — 25<br>Засыпка керамзитовая сухая фр. 0–5 (в слое — выпуски К1) — 110<br>Плита перекрытия монолитная<br>Всего 155 мм; ЧП −0,015, верх плиты −0,170 | 6,88 |
| 5, 7 | 3 |  | Керамогранит 600×600×10 — 10<br>Клей плиточный С2 TE S1 — 5<br>Стяжка ЦПС М300 (В22,5), фибра, по звукоизоляции — 55<br>Звукоизоляция — минплита 110 кг/м³ 20<br>Засыпка керамзитовая фр. 0–5, уплотнённая — 80<br>Плита перекрытия монолитная<br>Всего 170 мм; ЧП ±0,000, верх плиты −0,170 | 12,34 |
| 6 | 4 |  | Инженерная доска дуб на клею — 14<br>Клей паркетный МС-полимерный — 1<br>Гидроизоляция полиуретановая, 2 слоя (зона мойки и острова) — 2<br>Стяжка ЦПС М300 (В22,5), фибра, по звукоизоляции — 53<br>Звукоизоляция — минплита 110 кг/м³ 20<br>Засыпка керамзитовая фр. 0–5, уплотнённая — 80<br>Плита перекрытия монолитная<br>Всего 170 мм; ЧП ±0,000, верх плиты −0,170 | 15,19 |
| 13 | 5 |  | Керамогранит 600×600×10 — 10<br>Клей плиточный С2 TE S1 (деформируемый) — 5<br>Сборное основание ГВЛВ 2×12,5 — 25<br>Пенополистирол экструзионный 2×50 100<br>Плита перекрытия монолитная<br>Всего 140 мм; ЧП −0,030, верх плиты −0,170 | 3,70 |
| | | | **Итого** | **106,37** |

## Примечания


1. За отметку ±0,000 принят чистый пол, не существующий (блок отметок). Площади — по чистым размерам помещений, м²; размеры — в мм.
2. Стык разнотипных покрытий — по оси дверного полотна (под полотном в закрытом положении); решение стыка — по ведомости стыков.
3. Размеры помещений в свету (ширина × длина, мм), не поместившиеся на плане: пом. 5 — 4090 × 1110; пом. 8 — 1360 × 950; пом. 9 — 3590 × 3010, 2580 × 60; пом. 10 — 950 × 1380; пом. 12 — 1340 × 2110.
4. Пол санузлов ниже смежных помещений на 15 мм за счёт меньшей толщины стяжки (верх плиты общий — по экспликации полов); гидроизоляция по стяжке с заведением на стены не менее 200 мм (СП 29.13330.2011, п. 7.2), до облицовки — тест проливом и акт скрытых работ.
5. Выпуски канализации с уклоном и трассы водоснабжения — в слое засыпки под стяжкой (по экспликации полов); отметки, уклоны и прочистки — по листу разводки ВК 23.
6. Штучные покрытия (инженерная доска): направление — по стрелке; влажность основания по СМ не более 2,0 % (по ТУ изготовителя).
7. Ровность основания — просвет под 2-метровой рейкой не более 2 мм: пом. 1, 3, 4, 6, 8, 9, 11, 12 (инженерная доска), пом. 2, 5, 7, 10 (керамогранит); 3 мм: пом. 13 (керамогранит); проверить до укладки покрытия (СП 71.13330.2017, табл. 8.5).
8. Плавающая стяжка по звукоизоляции: демпферная (кромочная) лента по контуру помещения, у стояков и колонн — до верха чистого пола (СП 51.13330.2011, п. 9.11); плинтус крепится только к стене.
9. Сетка на плитке — условная, в размер формата; точка старта и раскладка — по листу раскладки плитки.
10. Узор покрытия (заливка-код типа пола) прерывается под надписями — площадями помещений и отметками чистого пола.
11. Электрический тёплый пол: ТП1 — пом. 2, мат 1755×780 мм, 205 Вт; ТП2 — пом. 10, мат 490×620 мм, 50 Вт; контуры показаны пунктиром; датчик температуры (Д) — в гофротрубе, трасса к терморегулятору — по обмеру. Марка мата и точное положение датчика — при закупке и по обмеру.
12. Пироги полов — по экспликации полов: слои сверху вниз, толщины в мм; гидроизоляция мокрых зон — в пироге и в ведомости отделки; схема пола — без масштаба.

| | | | | | | |
|---|---|---|---|---|---|---|
| | | | | | Проект: Четырёхкомнатная квартира | **М 1:75** |
| | Лист | № док. | Подпись | Дата | План покрытий пола | Стадия: П; Лист: 50; Листов: 120 |
| Дизайнер | Кырлан А.С. | | | 04.11.26 | | |


**Фрагмент 1. Ванная комната (пом. 2). Пол 600×600, шов 2 мм, М 1:50**

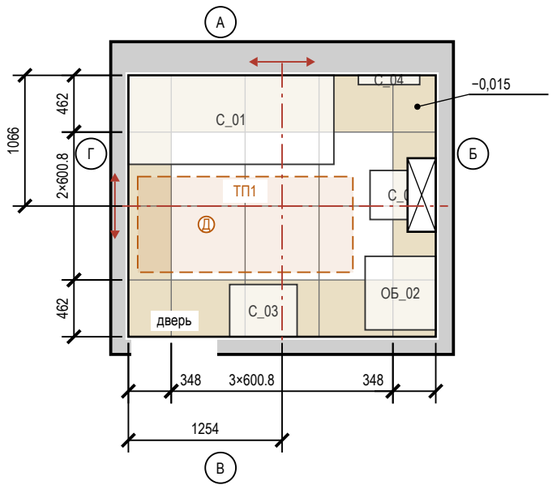



**Фрагмент 2. Коридор (пом. 5). Пол 600×600, шов 2 мм, М 1:50**

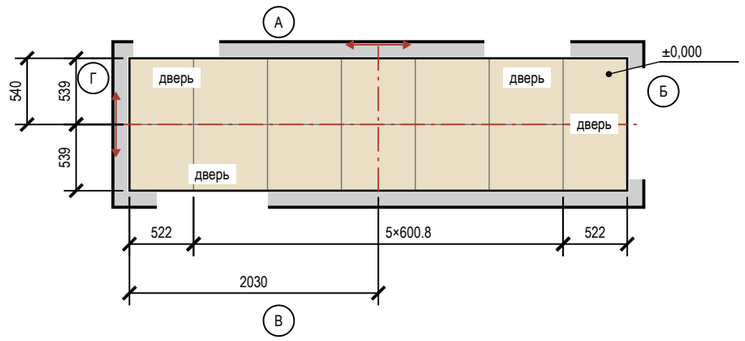


**Фрагмент 3. Прихожая-коридор (пом. 7). Пол 600×600, шов 2 мм, М 1:50**

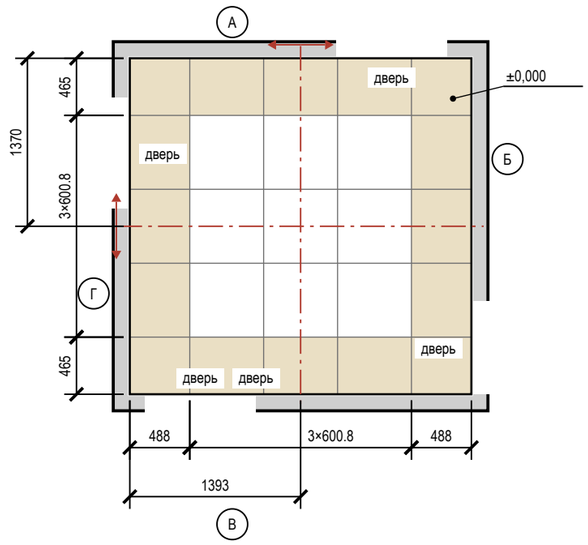


**Фрагмент 4. Санузел (пом. 10). Пол 600×600, шов 2 мм, М 1:50**

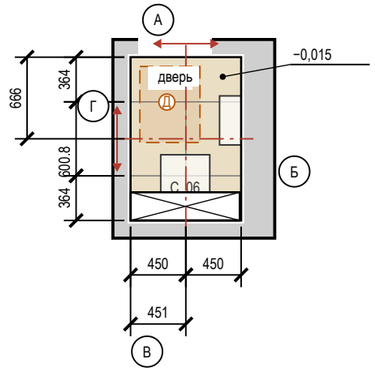


## Ведомость материалов

| Материал | Класс, код | Норма расхода | Кол-во |
|---|---|---|---|
| Затирка | CG2WA аналог: Mapei Ultracolor 133 | (a+b)/ab·шов·t·1,6 | 5,6 кг |
| Затирка | CG2WA | (a+b)/ab·шов·t·1,6 | 0,1 кг |
| Клей | C2 TE S1 аналог: Litokol K80 Eco | 1,5 кг/м²·мм, слой 5 | 425 кг (17 меш.) |
| Клей | C2 TE S1 | 1,5 кг/м²·мм, слой 5 | 10 кг (1 меш.) |
| Гидроизоляция | обмазочная, 2 слоя: пол, стены по периметру и зоны замачивания | по ТУ | 16,2 м² |
| Демпф. лента | по периметру пола из плитки | | 29,1 м |

## Ведомость плитки

| Помещение, поверхность | Плитка, код | Формат | Шов | S, м² | Целых | Подр. | С запасом |
|---|---|---|---|---|---|---|---|
| Ванная комната, пол | керамогранит матовый R10, тон J484 | 600.8×600.8 | 2 | 5,57 | 6 | 14 | 22 |
| Ванная комната, стены А–Г | керамогранит матовый, тон F497 | 600.8×600.8 | 2 | 21,66 | 23 | 67 | 100 |
| Ванная комната, короб инсталляции | керамогранит матовый, тон F497 | 600.8×600.8 | 2 | 1,36 | 1 | 6 | 8 |
| Коридор, пол | керамогранит матовый R10, тон V486 | 600.8×600.8 | 2 | 4,54 | 0 | 14 | 16 |
| Прихожая-коридор, пол | керамогранит матовый R10, тон V486 | 600.8×600.8 | 2 | 7,80 | 9 | 16 | 28 |
| Санузел, пол | керамогранит матовый R10, тон J484 | 600.8×600.8 | 2 | 1,31 | 0 | 6 | 7 |
| Санузел, стены А–Г | керамогранит матовый, тон F497 | 600.8×600.8 | 2 | 9,44 | 6 | 44 | 56 |
| Санузел, короб инсталляции | керамогранит матовый, тон F497 | 600.8×600.8 | 2 | 1,76 | 0 | 10 | 11 |
| Кухня, фартук (ст. А) | аналог: керамогранит матовый, тон F497 | 600.8×600.8 | 2 | 1,11 | 1 | 3 | 5 |
| **Итого 600.8×600.8** | | | | **54,54** | **46** | **180** | **253** |

## Условные обозначения

- плитка целая; тонкая линия — шов
- плитка с подрезкой (размер — на цепочке)
- ось старта; стрелки — направление укладки
- сантехприбор: габарит, высота по практике
- короб инсталляции: плитка пола — до короба
- электрический тёплый пол: контур мата ТП, Д — датчик
- отметка чистого пола на полке выноски, м
- А — обозначение стены А–Г (как на развёртках)

## Примечания

1. Раскладка от чистовых размеров: стены санузлов теряют 10 + 5 + 9 = 24 мм на сторону (штукатурка, клей, плитка); подрезки — чистые, без шва.
2. Старт — от центра помещения (штрихпунктир, стрелки — направление укладки); размер старта — от чистовых стен Г и А.
3. Раскладка фартука «Кухня» — на листе «Раскладка плитки. Фартук кухни».
4. Количество: целые по раскладке + по одной на подрезку, запас 10 %; один артикул — одна партия и тон. Исключены поддон, короб, проёмы и места за коробом; S — по чистым граням: стены нетто = зона облицовки по ведомости отделки − место за коробом инсталляции 1,71 м² (плитку за коробом не кладут), короб — отдельной строкой.
5. Клей C2 TE S1 аналог: Litokol K80 Eco; C2 TE S1 (ГОСТ Р 56387-2018), затирка CG2WA аналог: Mapei Ultracolor 133; CG2WA; расход — по ТУ выбранной марки.
6. Гидроизоляция: пол и стены 200 мм от ЧП; над ванной — до 2100 и 300 мм за борт (пом. 2) (см. развёртки); акт скрытых работ, пролив 24 ч.
7. Электрический тёплый пол: ТП1 — пом. 2, мат 1755×780 мм, 205 Вт; ТП2 — пом. 10, мат 490×620 мм, 50 Вт; контуры показаны пунктиром; датчик температуры (Д) — в гофротрубе, трасса к терморегулятору — по обмеру. Марка мата и точное положение датчика — при закупке и по обмеру. Плитку над матом клеить клеем, который изготовитель допускает для тёплого пола, до включения выдержать срок по ТУ клея.
8. Швы пола совмещены со швами стены А; по периметру — демпферная лента.
9. Отметка чистого пола −0,015, порог 15 мм; стык с соседним покрытием — по оси полотна двери.


| | | | | |
|---|---|---|---|---|
| | | | | |
| | Лист | № док. | Подпись | Дата |
| Дизайнер | Кырлан А.С. | | | 04.11.26 |

Проект: Четырёхкомнатная квартира — **М 1:50**

Раскладка плитки. Планы полов

| Стадия | Лист | Листов |
|---|---|---|
| П | 51 | 120 |

**Фрагмент 1. Кухня (пом. 6), фартук, стена А. 600×600, шов 2 мм, М 1:20**

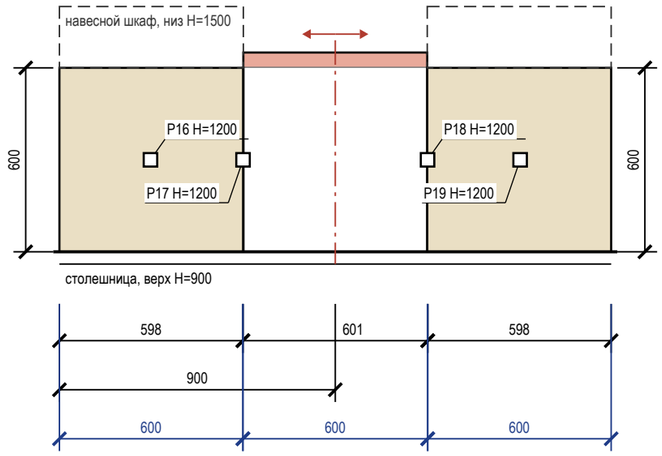


## Условные обозначения

- плитка целая; тонкая линия — шов
- плитка с подрезкой (размер — на цепочке)
- ось старта; стрелки — направление укладки
- электроточка: марка и Н — по листам ЭОМ
- столешница (верх)
- навесной шкаф над фартуком

## Подсчёт плитки


| Поверхность | Формат | S, м² | Целых | Подр. | С запасом |
|---|---|---|---|---|---|
| Кухня, фартук (ст. А) | 600×600 | 1,11 | 1 | 3 | 5 |

## Примечания


1. Фартук, Кухня: 600×600 горизонтально, шов 2 мм; зоны 600 мм — 900…1500, 600 мм — 900…1550, 600 мм — 900…1500 (от столешницы до низа навесного шкафа, без шкафа — 650 мм). Старт от центра участка, подрезки 598 мм. Площадь 1,11 м² — как в ведомости отделки.
2. Фартук — после монтажа столешницы, низ на 2–3 мм выше неё, шов со столешницей — санитарный герметик; навесные шкафы — после фартука. Торцы у пенала и стены — профиль или запил 45°.
3. Фартук, Кухня: в зоне до отм. 1550 верхний ряд подрезан 47 мм — меньше 1/3 плитки; полоса прикрыта корпусом навесного модуля и на виду не остаётся. Раскладкой не снимается: убрать подрезку можно, только выровняв низ этого модуля с соседними (1500 мм) — решение мебельщика.
4. Клей, затирка и итог по форматам — в ведомостях листа «Раскладка плитки. Планы полов».

| | | | | | | |
|---|---|---|---|---|---|---|
| | | | | | Проект: Четырёхкомнатная квартира | М 1:20 |
| | Лист | № док. | Подпись | Дата | | |
| Дизайнер | Кырлан А.С. | | | 04.11.26 | Раскладка плитки. Фартук кухни | Стадия: П; Лист: 52; Листов: 120 |

## Развёртка стены А

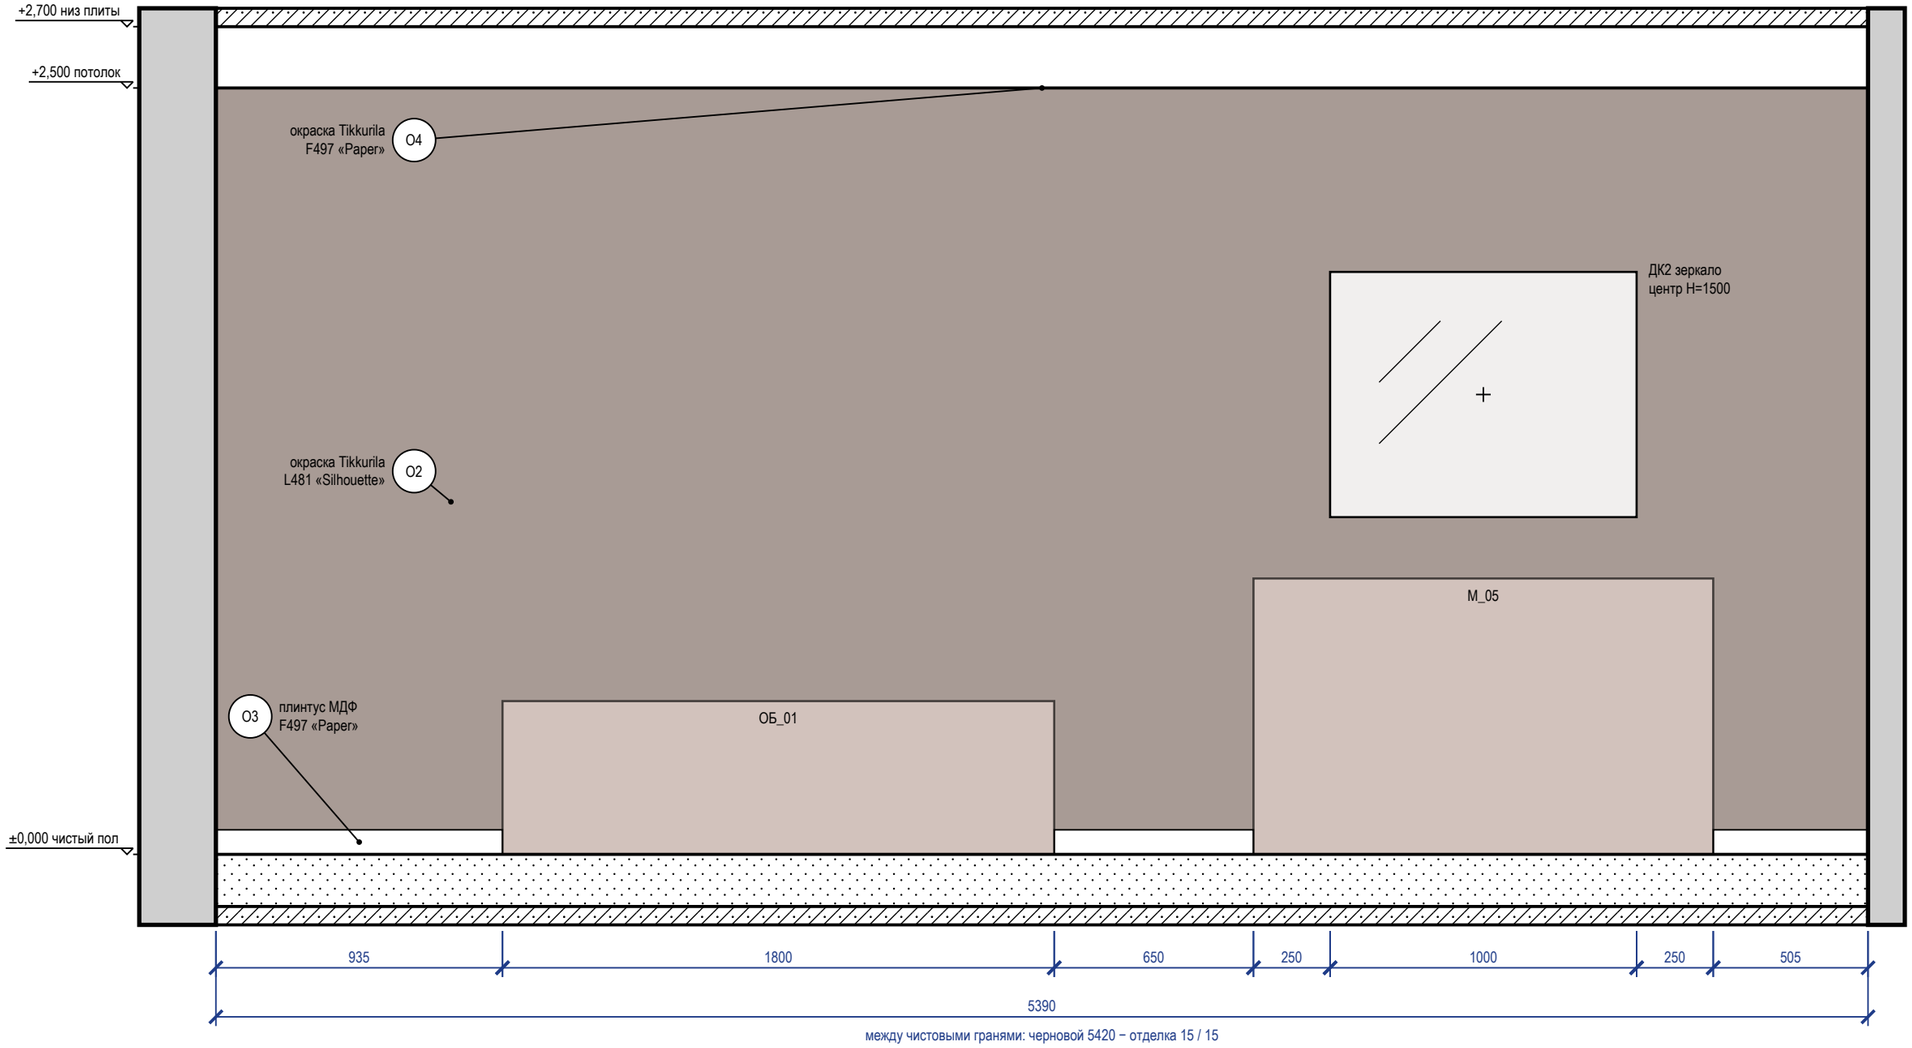


### Схема развёрток (М 1:100)

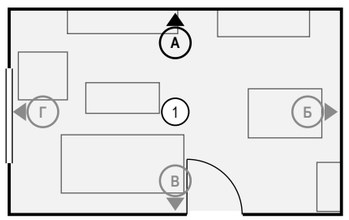


### Ведомость отделки (на листе)


| Марка | Поверхность | Материал, изделие | Цвет, код | Кол. |
|---|---|---|---|---|
| О2 | акцентная стена | окраска, Tikkurila Optiva 5 Matt, аналог: интерьерная краска, класс 2 по EN 13300, глубокоматовая/матовая, база С, матовая, подготовка К3 | Tikkurila L481 «Silhouette» | 13,5 м² |
| О3 | плинтус | плинтус МДФ, h 80 мм, аналог: плинтус МДФ под окраску 80×16 мм, полуглянцевая | Tikkurila F497 «Paper» | 2,1 м |
| О4 | потолок | окраска, Tikkurila Anti-Reflex 2, глубокоматовая, подготовка Q3 | Tikkurila F497 «Paper» | 18,2 м² |

### Примечания

1. Размеры — в мм от чистовых поверхностей стен; условные обозначения и общие указания — лист 3.
2. Стена А показана двумя видами: здесь — архитектурная развёртка (мебель, отделка, проёмы, высоты), электроточки и выводы ВК с привязками и таблицей — на листе 54 («Привязки»).
3. Картины и зеркала крепить к основанию по паспорту изделия (закладные и анкеры — в перечне скрытых работ); крест — ось центра предмета.
4. Потолок — у каждой стены свой, по плану потолков (ПТ1); ступени — зоной, кромка короба перед нишей — тонкой линией; в поле потолка: ПТ2 +2,600.

| | | | | | | |
|---|---|---|---|---|---|---|
| | | | | | Проект: Четырёхкомнатная квартира | М 1:20 |
| | Лист | № док. | Подпись | Дата | | |
| Дизайнер | Кырлан А.С. | | | 04.11.26 | Развёртка стены А. Зал (пом. 1) | Стадия: П; Лист: 53; Листов: 120 |

## Развёртка стены А: электроточки и выводы

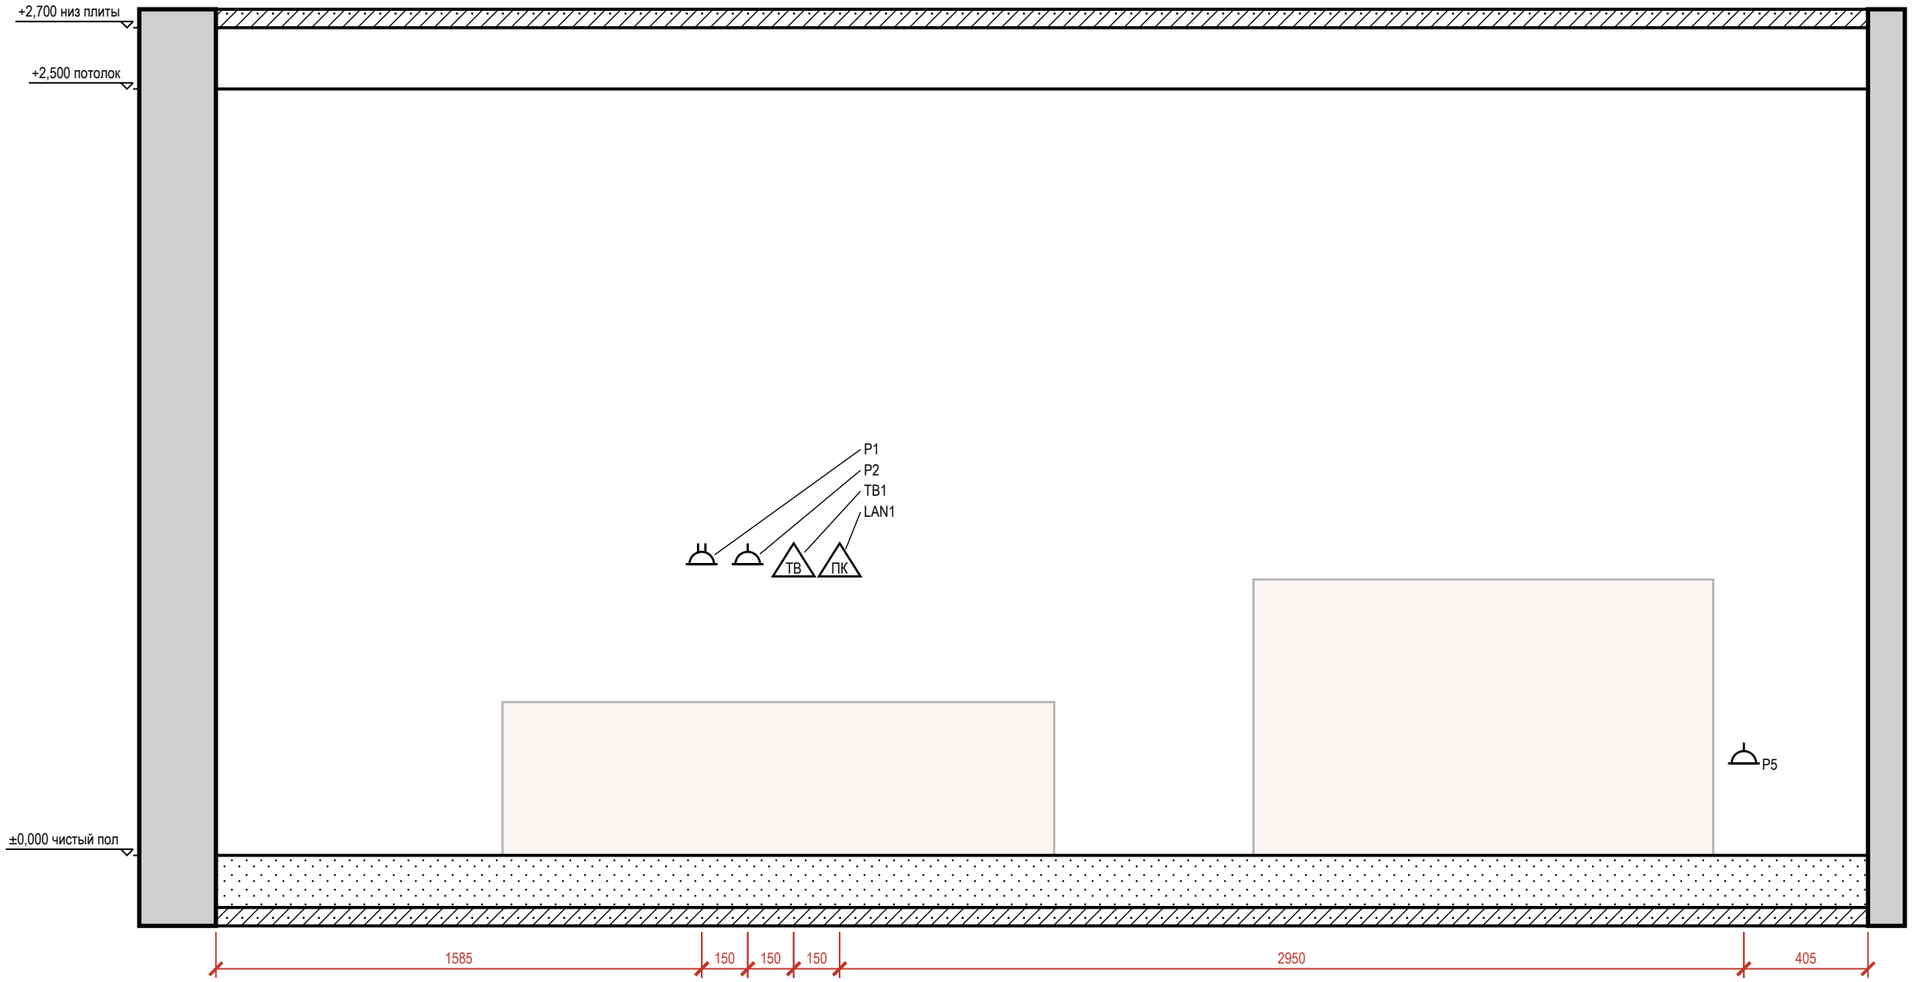



### Таблица привязок электроточек и выводов

| Марка | Назначение | От угла, мм | Н от пола, мм | Примечание |
|---|---|---|---|---|
| P1 | розетка: ТВ-зона: телевизор, медиаплеер | 1585 | 950 | рамка 2 поста, гр. 5 |
| P2 | розетка: ТВ-зона: саундбар | 1735 | 950 | гр. 5 |
| TB1 | розетка ТВ: ТВ-зона | 1885 | 950 | |
| LAN1 | розетка RJ45: ТВ-зона | 2035 | 950 | |
| P5 | розетка: обеденная зона, буфет M_05 | 4985 | 300 | гр. 5 |

### Условные обозначения

- розетка с заземляющим контактом; у знака — марка, ×N постов в рамке, гр. — группа щита, Н — высота оси, мм
- ПК — розетка компьютерная RJ45
- ТВ — розетка телевизионная
- привязки точек и выводов от угла и от пола, мм
- А — марка развёртки: буква стены, стрелка — взгляд

### Схема развёрток (М 1:100)

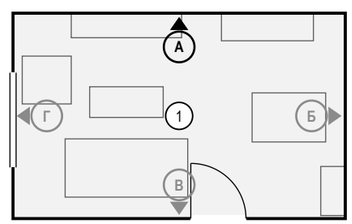



### Примечания

1. Вид «Привязки» стены А — электроточки и выводы ВК; архитектурная развёртка (мебель, отделка, проёмы, высоты) — на листе 53. Мебель и приборы — подложкой для ориентира; их марки и обозначения мебели, проёмов и стен — там же.
2. Привязки — в мм: по горизонтали от левого чистового угла стены до оси изделия, Н — от чистого пола до оси; все точки — в таблице привязок. Красная цепочка — привязки по осям; точки ближе 120 мм одна к другой в цепочку не дробятся — их привязки только в таблице.
3. У знака — марка электроточки (Р — розетка, S — выключатель, Св — светильник, ЭВ — вывод кабеля); условные обозначения и общие указания — лист 3.


| | | | | | |
|---|---|---|---|---|---|
| | | | | | Проект: Четырёхкомнатная квартира — М 1:20 |
| | Лист | № док. | Подпись | Дата | |
| Дизайнер | Кырлан А.С. | | | 04.11.26 | Привязки электроточек, стена А. Зал (пом. 1) |
| | | | | | Стадия: П; Лист: 54; Листов: 120 |

выпуск 04.11.2026 № b23f08ad9b · стр. 54 из 120

## Развёртка стены Б

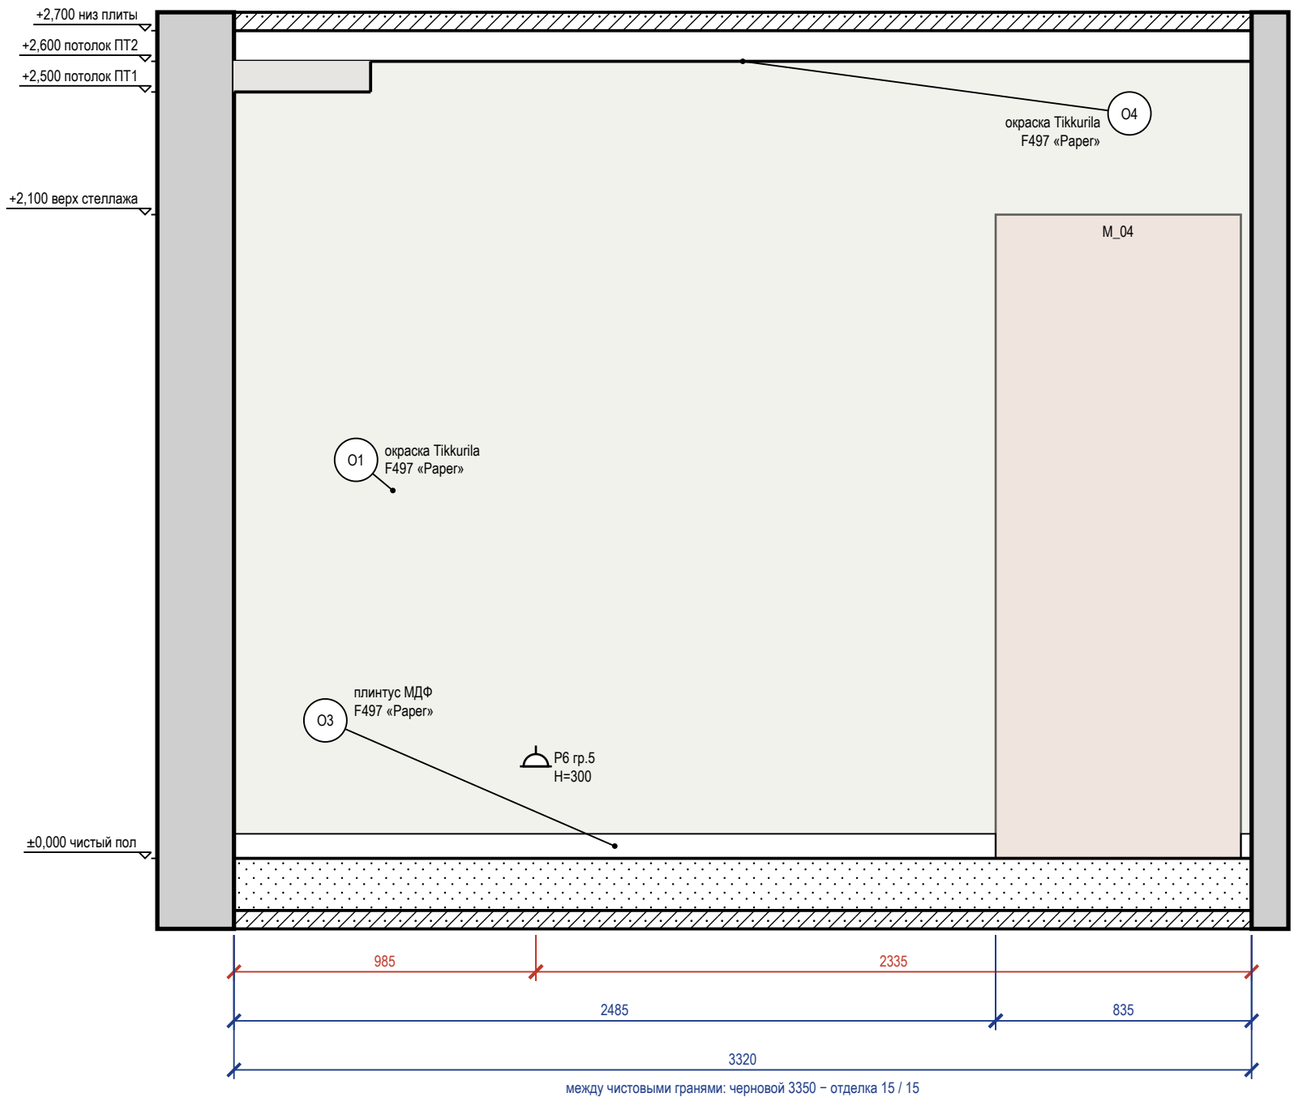


### Схема развёрток (М 1:100)

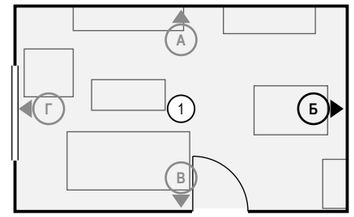


### Ведомость отделки (на листе)


| Марка | Поверхность | Материал, изделие | Цвет, код | Кол. |
|---|---|---|---|---|
| О1 | стены | окраска, Tikkurila Optiva 5 Matt, матовая, подготовка К3 | Tikkurila F497 «Paper» | 8,6 м² |
| О3 | плинтус | плинтус МДФ, h 80 мм, аналог: плинтус МДФ под окраску 80×16 мм, полуглянцевая | Tikkurila F497 «Paper» | 2,5 м |
| О4 | потолок | окраска, Tikkurila Anti-Reflex 2, глубокоматовая, подготовка Q3 | Tikkurila F497 «Paper» | 18,2 м² |

### Примечания


1. Размеры — в мм от чистовых поверхностей стен; условные обозначения и общие указания — лист 3.
2. Потолок — у каждой стены свой, по плану потолков (ПТ2, ПТ1); ступени — зоной, кромка короба перед нишей — тонкой линией.

| | | | | | | |
|---|---|---|---|---|---|---|
| | | | | | Проект: Четырёхкомнатная квартира | М 1:20 |
| | Лист | № док. | Подпись | Дата | | |
| Дизайнер | Кырлан А.С. | | | 04.11.26 | Развёртка стены Б. Зал (пом. 1) | Стадия: П; Лист: 55; Листов: 120 |

## Развёртка стены В

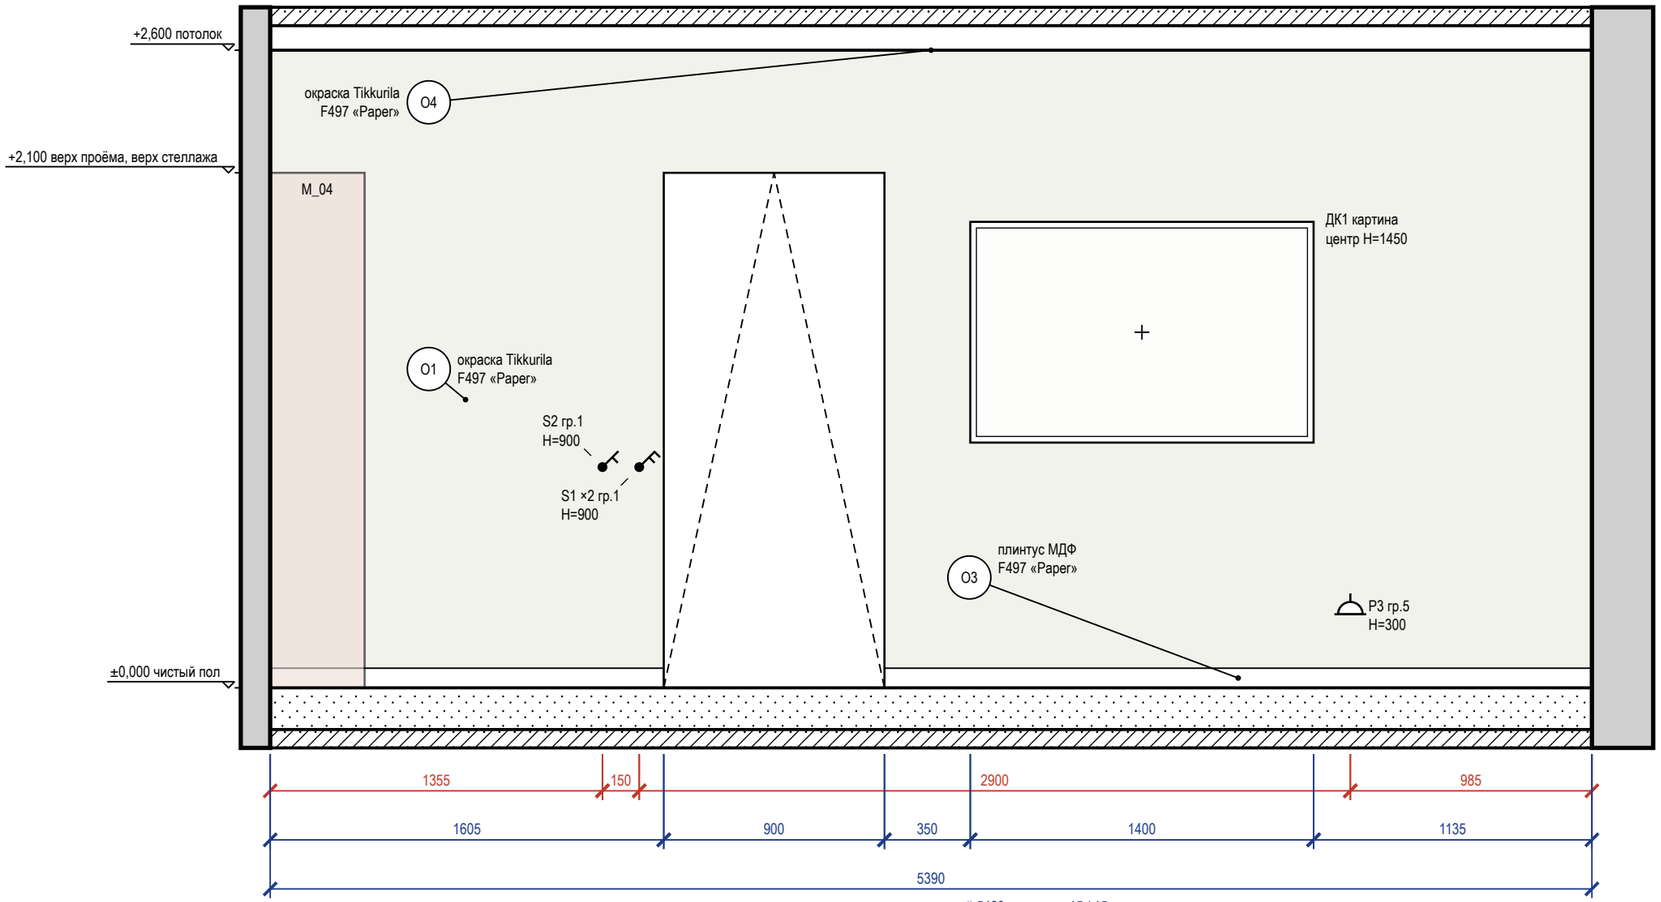


### Схема развёрток (М 1:100)

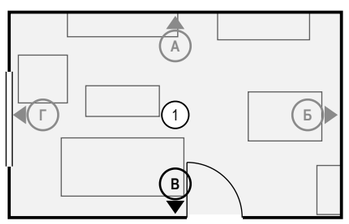


### Ведомость отделки (на листе)


| Марка | Поверхность | Материал, изделие | Цвет, код | Кол. |
|---|---|---|---|---|
| O1 | стены | окраска, Tikkurila Optiva 5 Matt, матовая, подготовка К3 | Tikkurila F497 «Paper» | 12,1 м² |
| O3 | плинтус | плинтус МДФ, h 80 мм, аналог: плинтус МДФ под окраску 80×16 мм, полуглянцевая | Tikkurila F497 «Paper» | 4,5 м |
| O4 | потолок | окраска, Tikkurila Anti-Reflex 2, глубокоматовая, подготовка Q3 | Tikkurila F497 «Paper» | 18,2 м² |

### Примечания


1. Размеры — в мм от чистовых поверхностей стен; условные обозначения и общие указания — лист 3.
2. Картины и зеркала крепить к основанию по паспорту изделия (закладные и анкеры — в перечне скрытых работ); крест — ось центра предмета.
3. Потолок — у каждой стены свой, по плану потолков (ПТ2); ступени — зоной, кромка короба перед нишей — тонкой линией; в поле потолка: ПТ1 +2,500.

| | | | | | | |
|---|---|---|---|---|---|---|
| | | | | | Проект: Четырёхкомнатная квартира | М 1:25 |
| | Лист | № док. | Подпись | Дата | Развёртка стены В. Зал (пом. 1) | Стадия / Лист / Листов |
| Дизайнер | Кырлан А.С. | | | 04.11.26 | | П / 56 / 120 |

## Развёртка стены Г

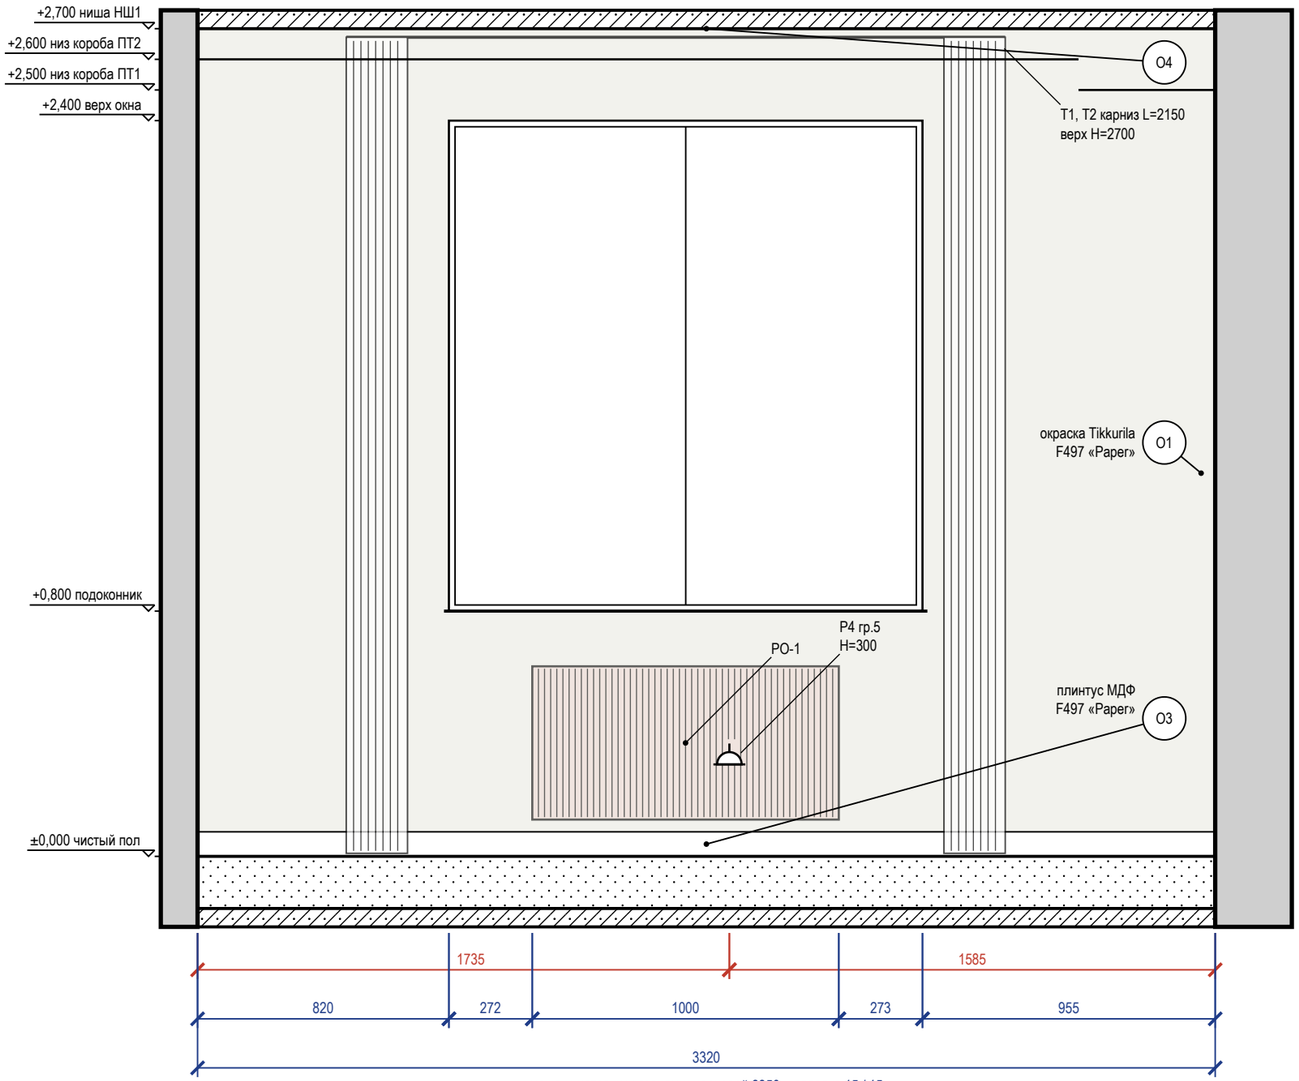


## Схема развёрток (М 1:100)

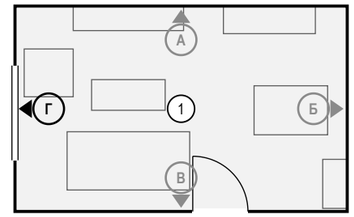


## Ведомость отделки (на листе)


| Марка | Поверхность | Материал, изделие | Цвет, код | Кол. |
|---|---|---|---|---|
| О1 | стены | окраска, Tikkurila Optiva 5 Matt, матовая, подготовка К3 | Tikkurila F497 «Paper» | 6,5 м² |
| О3 | плинтус | плинтус МДФ, h 80 мм, аналог: плинтус МДФ под окраску 80×16 мм, полуглянцевая | Tikkurila F497 «Paper» | 3,3 м |
| О4 | потолок | окраска, Tikkurila Anti-Reflex 2, глубокоматовая, подготовка Q3 | Tikkurila F497 «Paper» | 18,2 м² |

## Примечания

1. Размеры — в мм от чистовых поверхностей стен; условные обозначения и общие указания — лист 3.
2. Карнизы (шины) — по ведомости текстиля декоратора: длина L и верх H на развёртке — те же числа, что в ведомости; крепление — до окраски потолка.
3. Потолок — у каждой стены свой, по плану потолков (НШ1, ПТ2, ПТ1); ступени — зоной, кромка короба перед нишей — тонкой линией.
4. Линии узора (швы плитки, складки штор, рёбра радиаторов) прерываются у знаков и выносок — просвет между линиями не менее 0,7 мм.


| | | | | | | |
|---|---|---|---|---|---|---|
| | | | | | Проект: Четырёхкомнатная квартира | М 1:20 |
| | Лист | № док. | Подпись | Дата | | |
| Дизайнер | Кырлан А.С. | | | 04.11.26 | Развёртка стены Г. Зал (пом. 1) | Стадия: П; Лист: 57; Листов: 120 |

## Развёртка стены А

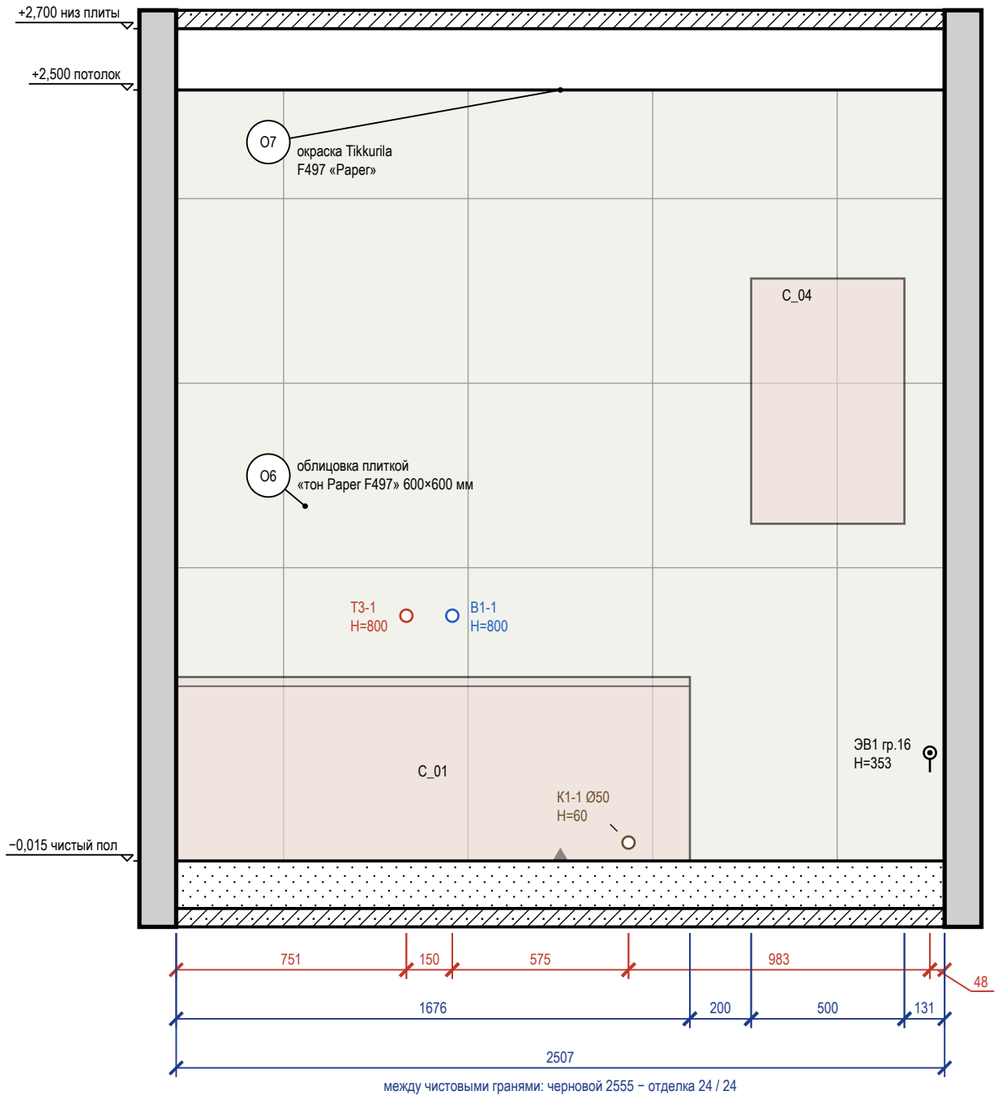



между чистовыми гранями: черновой 2555 − отделка 24 / 24

## Развёртка стены Б

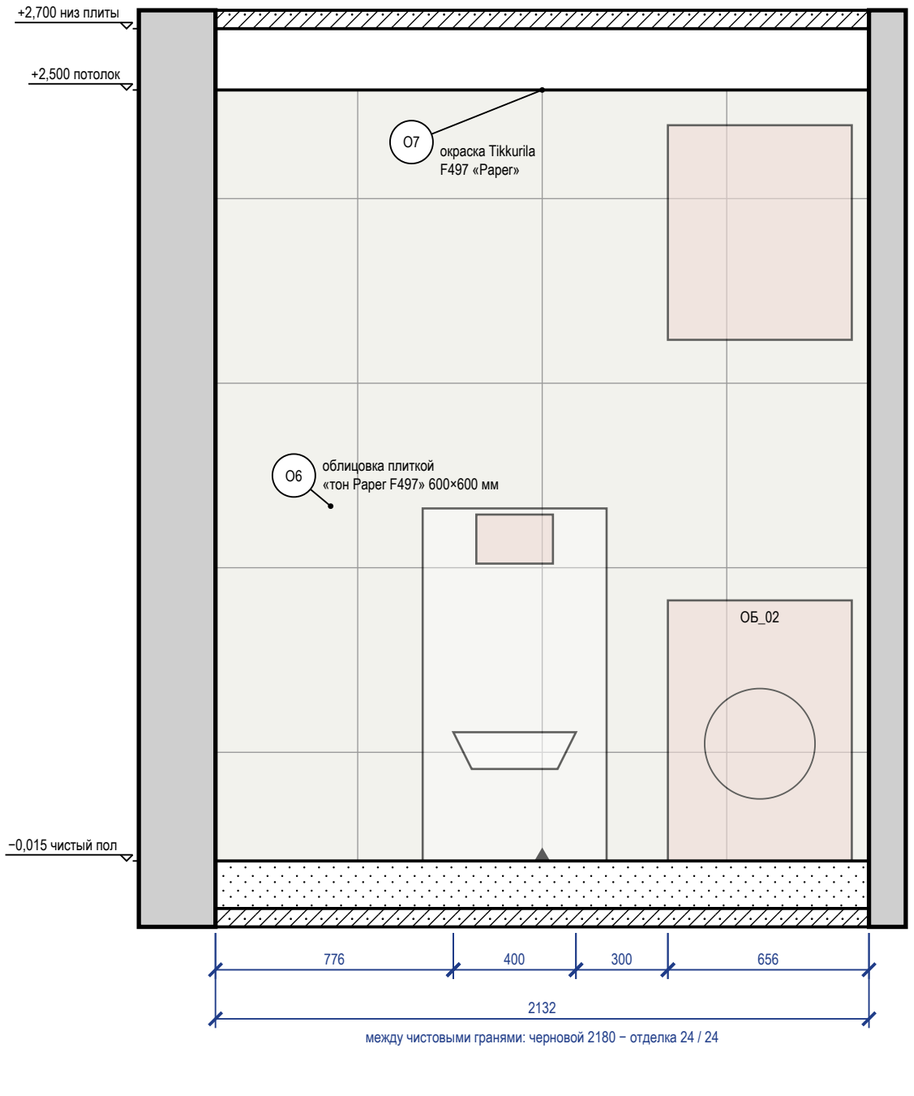


между чистовыми гранями: черновой 2180 − отделка 24 / 24

### Схема развёрток (М 1:100)

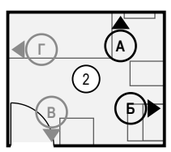


### Ведомость отделки (на листе)

| Марка | Поверхность | Материал, изделие | Цвет, код | Кол. |
|---|---|---|---|---|
| О6 | стены | облицовка плиткой, 600×600×9 мм, аналог: керамогранит матовый, тон F497, затирка CG2WA | #F1F1EC «тон Paper F497» | 11,7 м² |
| О7 | потолок | окраска, Tikkurila Luja 7, матовая, подготовка Q3 | Tikkurila F497 «Paper» | 5,6 м² |

### Примечания


1. Размеры — в мм от чистовых поверхностей стен; условные обозначения и общие указания — лист 3.
2. Стена Б показана двумя видами: здесь — архитектурная развёртка (мебель, отделка, проёмы, высоты), электроточки и выводы ВК с привязками и таблицей — на листе 60 («Привязки»).
3. Схема мебели, приборов и декора не является технической документацией для производства мебели; габариты — по паспортам изделий.
4. Облицовка — по сетке швов 2 мм, раскладка от оси стены (треугольник у пола), по высоте — от середины облицовки, подрезки у пола и у потолка поровну; подрезки — по листу раскладки плитки.
5. Гидроизоляция в 2 слоя, заход на стены 200 мм; над ванной — до 2100 и 300 мм за борт — до облицовки, с актом скрытых работ и тестом проливом (узел — на листе узлов).

| | | | | | | |
|---|---|---|---|---|---|---|
| | | | | | Проект: Четырёхкомнатная квартира | М 1:20 |
| | Лист | № док. | Подпись | Дата | Развёртки стен А, Б. Ванная комната (пом. 2) | |
| Дизайнер | Кырлан А.С. | | | 04.11.26 | | |

| Стадия | Лист | Листов |
|---|---|---|
| П | 58 | 120 |


выпуск 04.11.2026 № b23f08ad9b · стр. 58 из 120

## Развёртка стены В

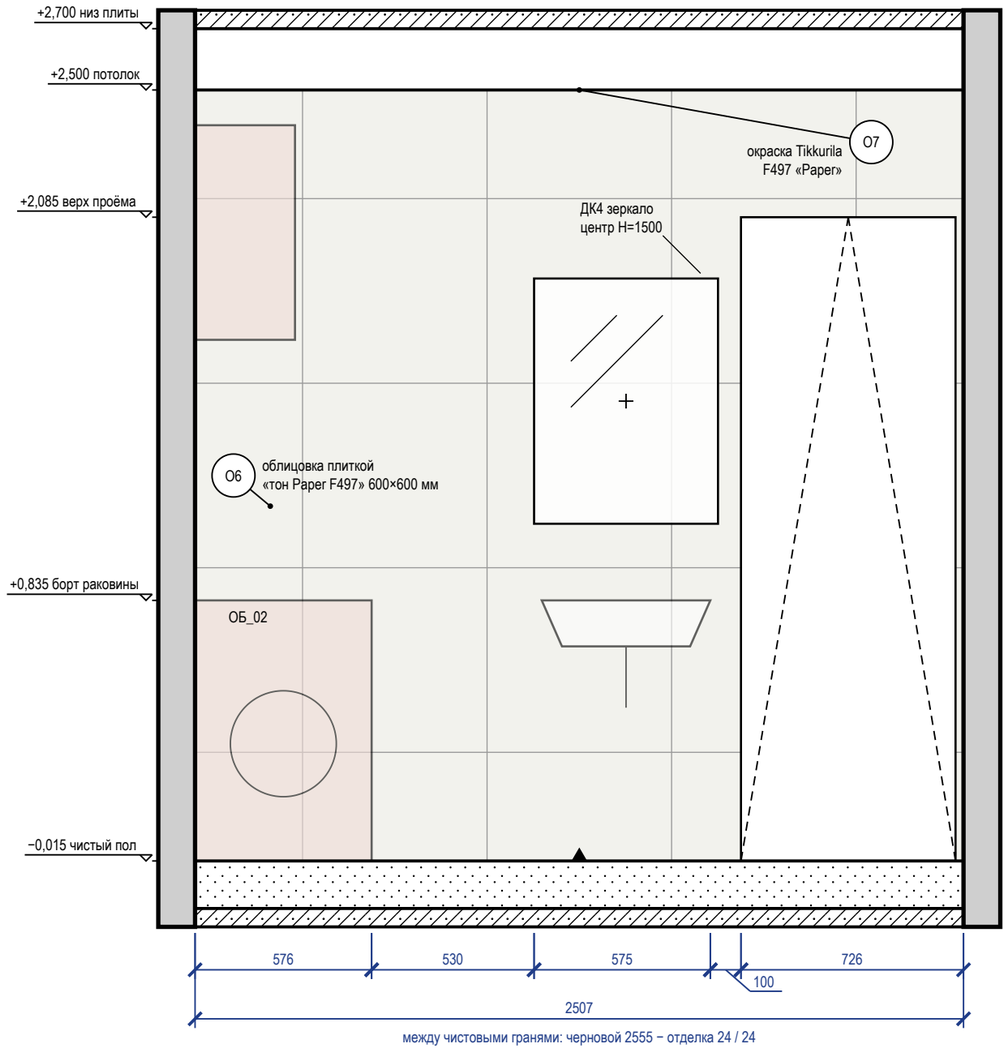



между чистовыми гранями: черновой 2555 − отделка 24 / 24

## Развёртка стены Г

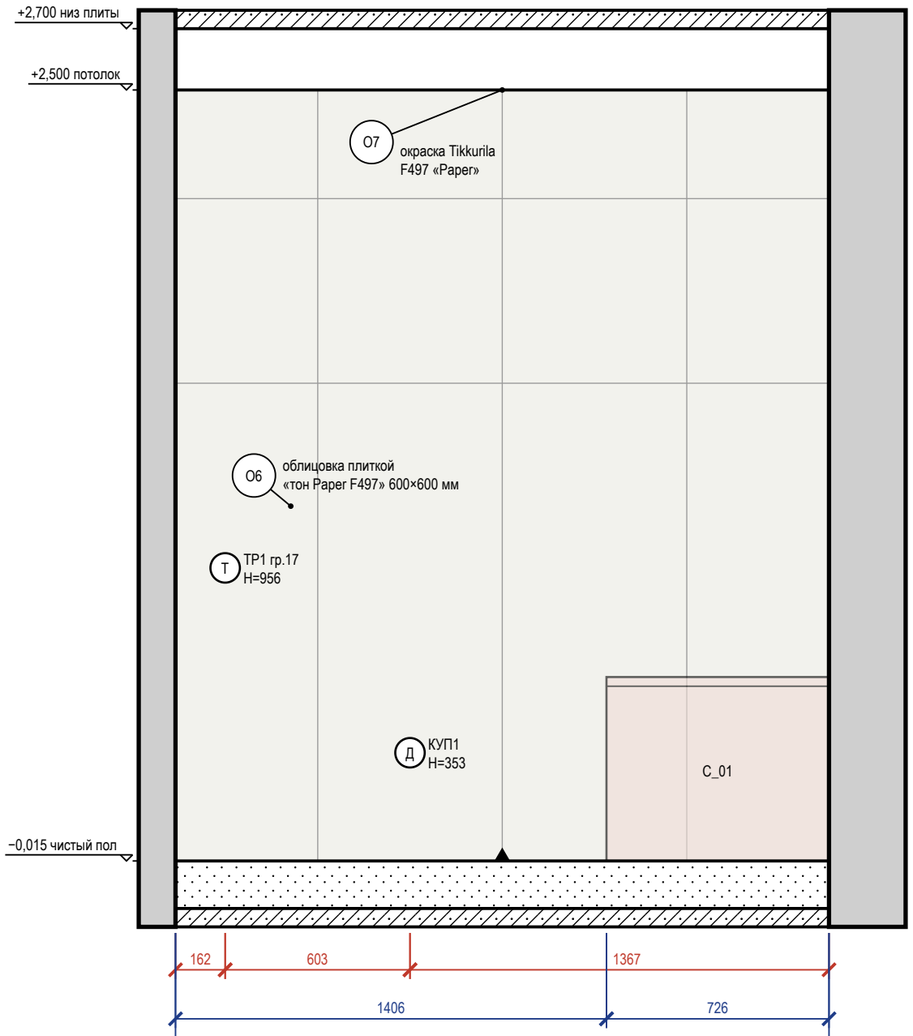


между чистовыми гранями: черновой 2180 − отделка 24 / 24

### Схема развёрток (М 1:100)

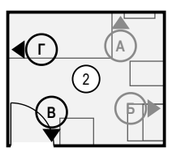


### Ведомость отделки (на листе)


| Марка | Поверхность | Материал, изделие | Цвет, код | Кол. |
|---|---|---|---|---|
| О6 | стены | облицовка плиткой, 600×600×9 мм, аналог: керамогранит матовый, тон F497, затирка CG2WA | #F1F1EC «тон Paper F497» | 10,2 м² |
| О7 | потолок | окраска, Tikkurila Luja 7, матовая, подготовка Q3 | Tikkurila F497 «Paper» | 5,6 м² |

### Примечания


1. Размеры — в мм от чистовых поверхностей стен; условные обозначения и общие указания — лист 3.
2. Стена В показана двумя видами: здесь — архитектурная развёртка (мебель, отделка, проёмы, высоты), электроточки и выводы ВК с привязками и таблицей — на листе 60 («Привязки»).
3. Схема мебели, приборов и декора не является технической документацией для производства мебели; габариты — по паспортам изделий.
4. Облицовка — по сетке швов 2 мм, раскладка от оси стены (треугольник у пола), по высоте — от середины облицовки, подрезки у пола и у потолка поровну; подрезки — по листу раскладки плитки.
5. Гидроизоляция в 2 слоя, заход на стены 200 мм; над ванной — до 2100 и 300 мм за борт — до облицовки, с актом скрытых работ и тестом проливом (узел — на листе узлов).
6. Картины и зеркала крепить к основанию по паспорту изделия (закладные и анкеры — в перечне скрытых работ); крест — ось центра предмета.

| | | | | | | |
|---|---|---|---|---|---|---|
| | | | | | Проект: Четырёхкомнатная квартира | М 1:20 |
| | Лист | № док. | Подпись | Дата | Развёртки стен В, Г. Ванная комната (пом. 2) | Стадия / Лист / Листов |
| Дизайнер | Кырлан А.С. | | | 04.11.26 | | П / 59 / 120 |

## Развёртка стены Б: электроточки и выводы

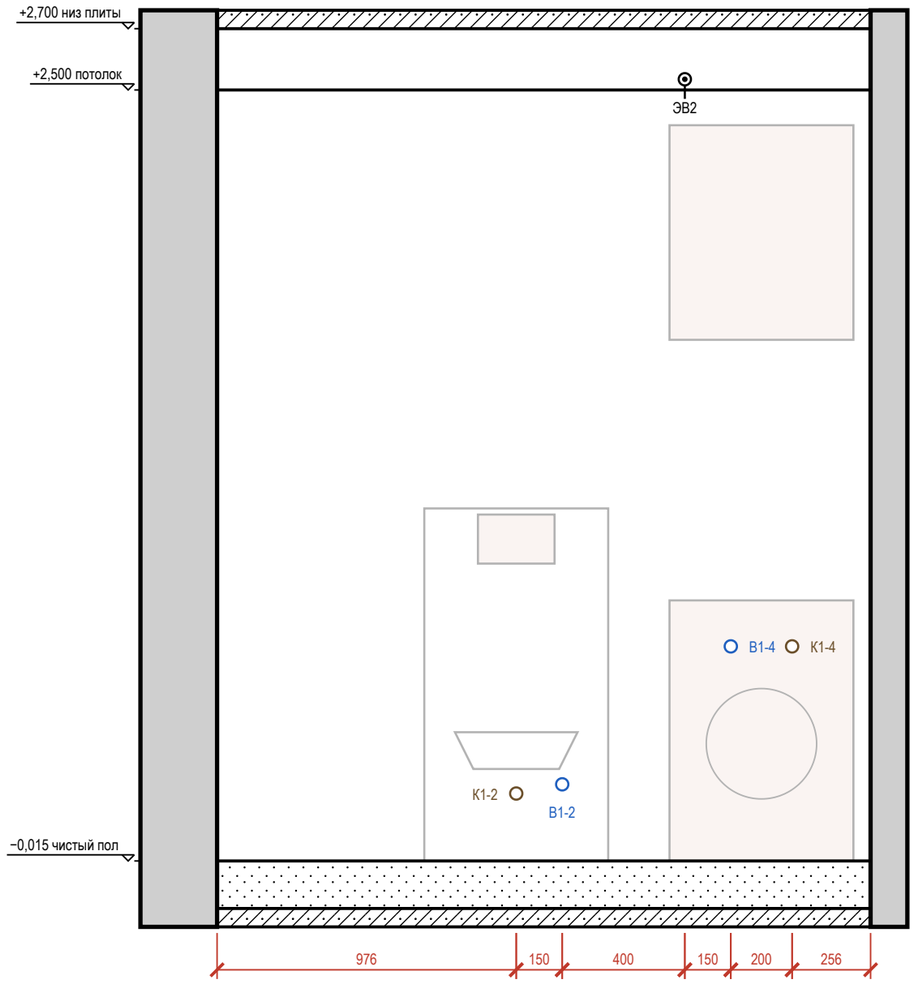


## Развёртка стены В: электроточки и выводы

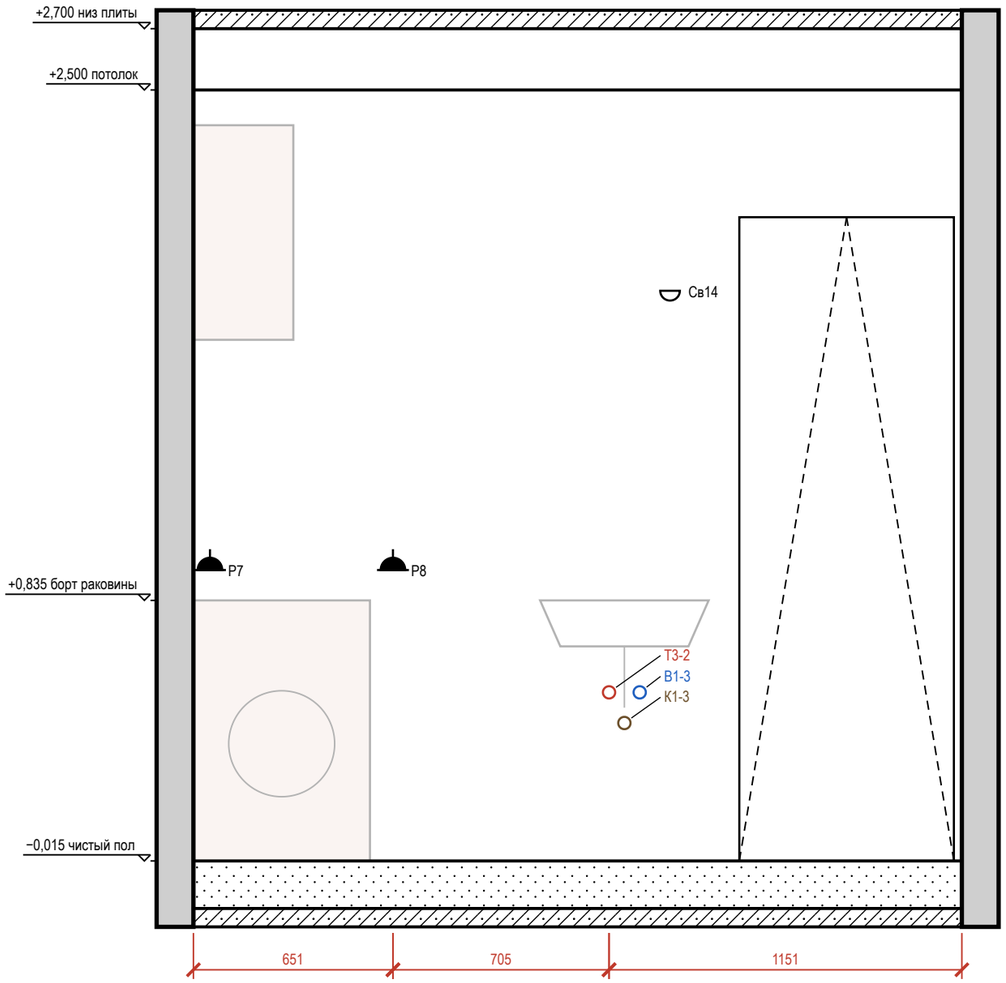


### Таблица привязок электроточек и выводов

| Стена | Марка | Назначение | От угла, мм | Н от пола, мм | Примечание |
|---|---|---|---|---|---|
| Б | К1-2 | канализация — унитаз подвесной | 976 | 220 | Ø110 |
| Б | В1-2 | холодная вода — унитаз подвесной | 1126 | 250 | в раме инсталляции |
| Б | ЭВ2 | вывод кабеля: вентилятор ВР1 (таймер выбега) | 1526 | 2550 | гр. 4 |
| Б | В1-4 | холодная вода — стиральная машина | 1676 | 700 | кран машины |
| Б | К1-4 | канализация — стиральная машина | 1876 | 700 | Ø40 |
| В | Р7 | розетка: стиральная машина | 48 | 949 | гр. 14, IP44 |

| Стена | Марка | Назначение | От угла, мм | Н от пола, мм | Примечание |
|---|---|---|---|---|---|
| В | Р8 | розетка: фен у умывальника | 651 | 949 | гр. 15, IP44 |
| В | Т3-2 | горячая вода — умывальник | 1356 | 550 | межос. 100 |
| В | К1-3 | канализация — умывальник | 1406 | 450 | Ø40 |
| В | В1-3 | холодная вода — умывальник | 1456 | 550 | межос. 100 |
| В | Св14 | светильник настенный | 1555 | 1860 | гр. 4 |

### Условные обозначения

- розетка влагозащищённая IP44
- вывод кабеля для подключения прибора (без розетки), марка ЭВ
- светильник настенный (бра), Н — высота оси
- вывод В1 (код — в ведомости привязок)
- вывод Т3 (код — в ведомости привязок)
- вывод К1 (код — в ведомости привязок)
- привязки точек и выводов от угла и от пола, мм


### Примечания

1. Вид «Привязки» стен Б, В — электроточки и выводы ВК; архитектурная развёртка (мебель, отделка, проёмы, высоты) — на листах 58, 59. Мебель и приборы подложкой для ориентира; их марки и обозначения мебели, проёмов и стен — там же.
2. Привязки — в мм: по горизонтали от левого чистового угла стены до оси изделия, Н — от чистого пола до оси; все точки — в таблице привязок. Красная цепочка — привязки по осям; точки ближе 120 мм одна к другой в цепочку не дробятся — их привязки только в таблице.
3. У знака — марка электроточки (Р — розетка, S — выключатель, Св — светильник, ЭВ — вывод кабеля); условные обозначения и общие указания — лист 3.
4. Коды выводов ВК: В1 — холодная вода, Т3 — горячая вода, К1 — канализация; номер после дефиса — номер вывода на листе выводов сантехники.

| | | | | | |
|---|---|---|---|---|---|
| | | | | | Проект: Четырёхкомнатная квартира — **М 1:20** |
| | Лист | № док. | Подпись | Дата | Привязки электроточек и выводов ВК, стены Б, В. Ванная комната (пом. 2) |
| Дизайнер | Кырлан А.С. | | | 04.11.26 | |


| Стадия | Лист | Листов |
|---|---|---|
| П | 60 | 120 |

## Развёртка стены А

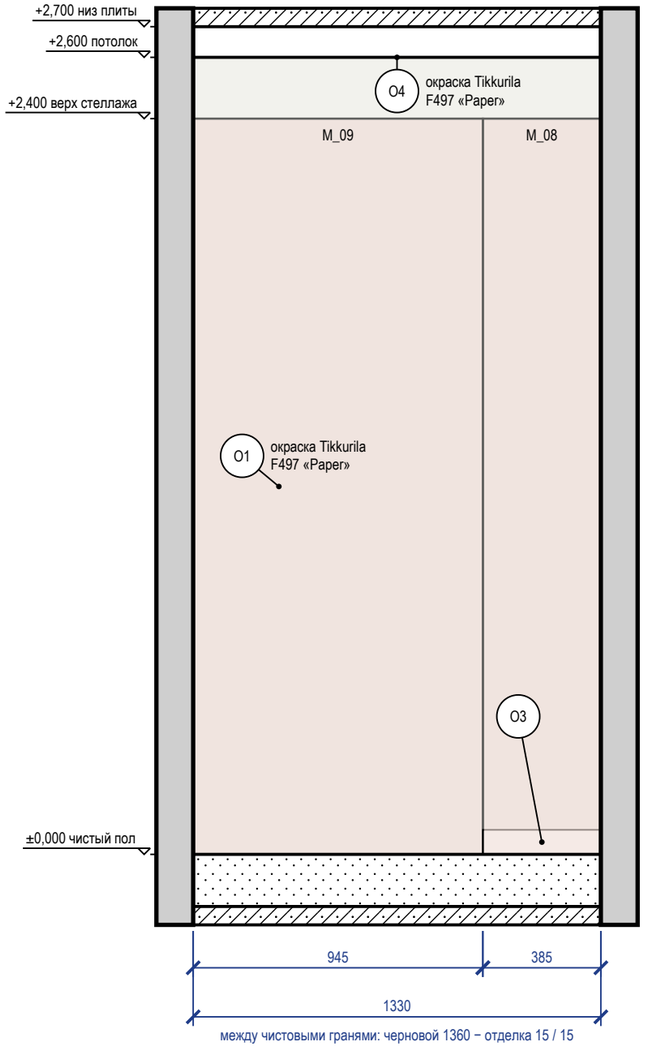



между чистовыми гранями: черновой 1360 − отделка 15 / 15

## Развёртка стены Б

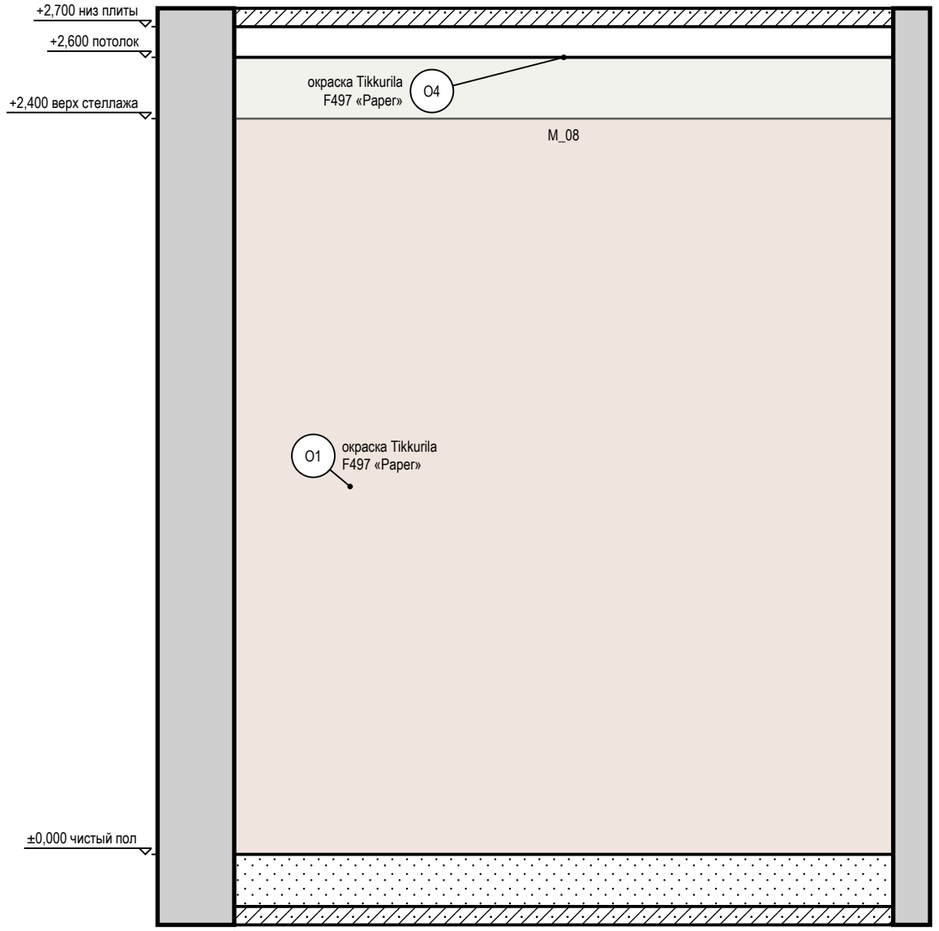



между чистовыми гранями: черновой 2180 − отделка 15 / 15

## Развёртка стены В

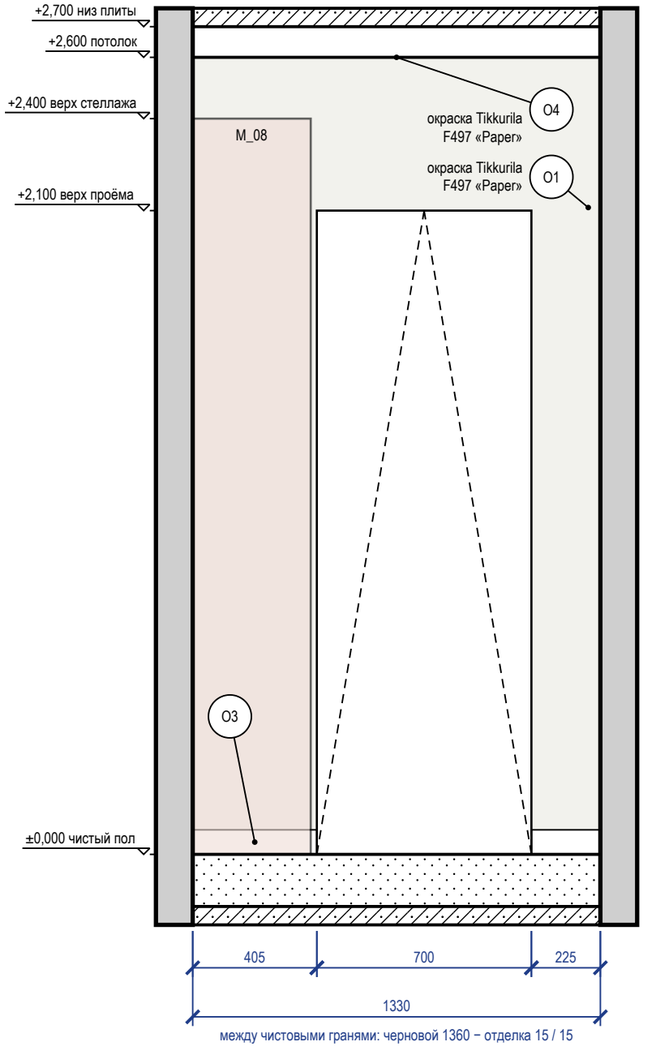


между чистовыми гранями: черновой 1360 − отделка 15 / 15

### Схема развёрток (М 1:100)

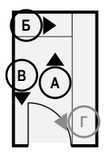


### Ведомость отделки (на листе)

| Марка | Поверхность | Материал, изделие | Цвет, код | Кол. |
|---|---|---|---|---|
| O1 | стены | окраска, Tikkurila Optiva 5 Matt, матовая, подготовка K3 | Tikkurila F497 «Paper» | 11 м² |
| O3 | плинтус | плинтус МДФ, h 80 мм, аналог: плинтус МДФ под окраску 80×16 мм, полуглянцевая | Tikkurila F497 «Paper» | 1 м |
| O4 | потолок | окраска, Tikkurila Anti-Reflex 2, глубокоматовая, подготовка Q3 | Tikkurila F497 «Paper» | 3 м² |


### Примечания

1. Размеры — в мм от чистовых поверхностей стен; условные обозначения и общие указания — лист 3.


| | | | | | | |
|---|---|---|---|---|---|---|
| | | | | | Проект: Четырёхкомнатная квартира | М 1:20 |
| | Лист | № док. | Подпись | Дата | Развёртки стен А, Б, В. Тёмная комната (пом. 3) | Стадия / Лист / Листов |
| Дизайнер | Кырлан А.С. | | | 04.11.26 | | П / 61 / 120 |

выпуск 04.11.2026 № b23f08ad9b · стр. 61 из 120

## Развёртка стены Г

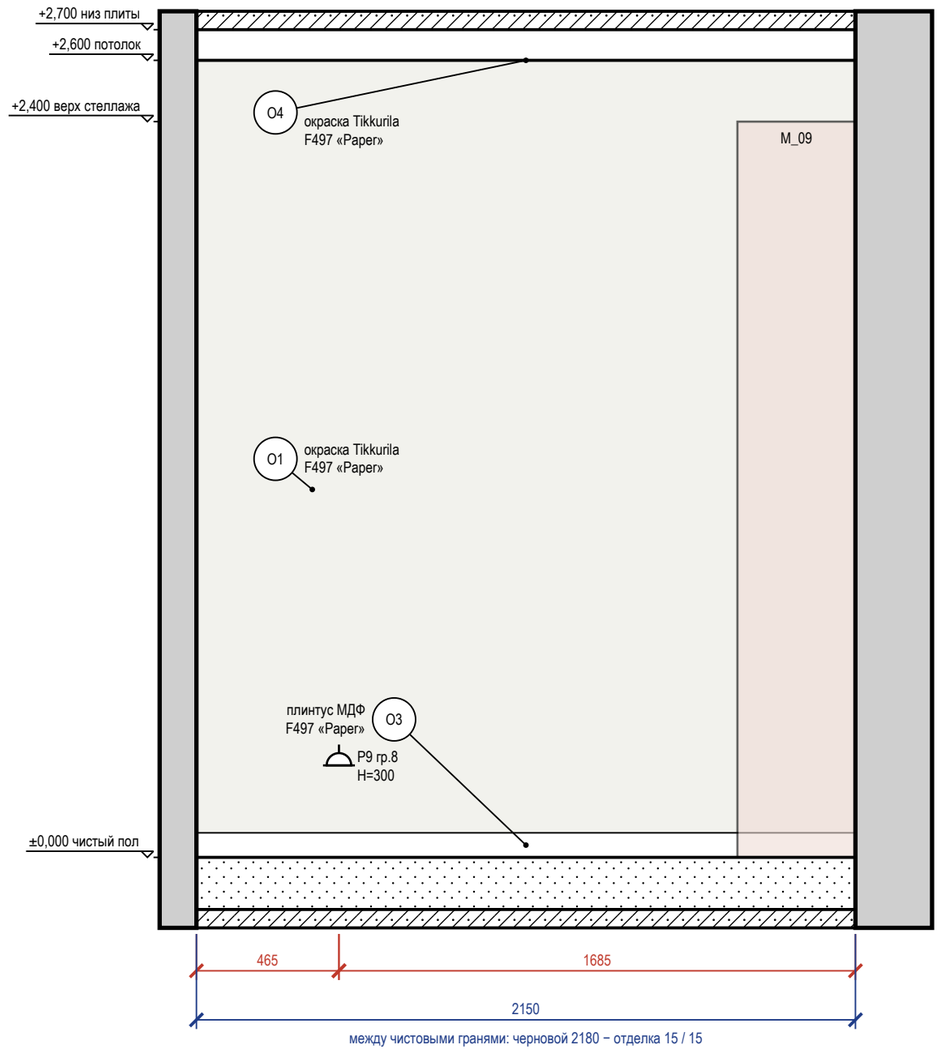


### Схема развёрток (М 1:100)

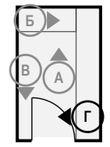


### Ведомость отделки (на листе)


| Марка | Поверхность | Материал, изделие | Цвет, код | Кол. |
|---|---|---|---|---|
| О1 | стены | окраска, Tikkurila Optiva 5 Matt, матовая, подготовка К3 | Tikkurila F497 «Paperг» | 5,6 м² |
| О3 | плинтус | плинтус МДФ, h 80 мм, аналог: плинтус МДФ под окраску 80×16 мм, полуглянцевая | Tikkurila F497 «Paperг» | 2,1 м |
| О4 | потолок | окраска, Tikkurila Anti-Reflex 2, глубокоматовая, подготовка Q3 | Tikkurila F497 «Paperг» | 3 м² |

### Примечания


1. Размеры — в мм от чистовых поверхностей стен; условные обозначения и общие указания — лист 3.

| | | | | | | |
|---|---|---|---|---|---|---|
| | | | | | Проект: Четырёхкомнатная квартира | М 1:20 |
| | Лист | № док. | Подпись | Дата | | |
| Дизайнер | Кырлан А.С. | | | 04.11.26 | Развёртка стены Г. Тёмная комната (пом. 3) | Стадия: П; Лист: 62; Листов: 120 |

## Развёртка стены А

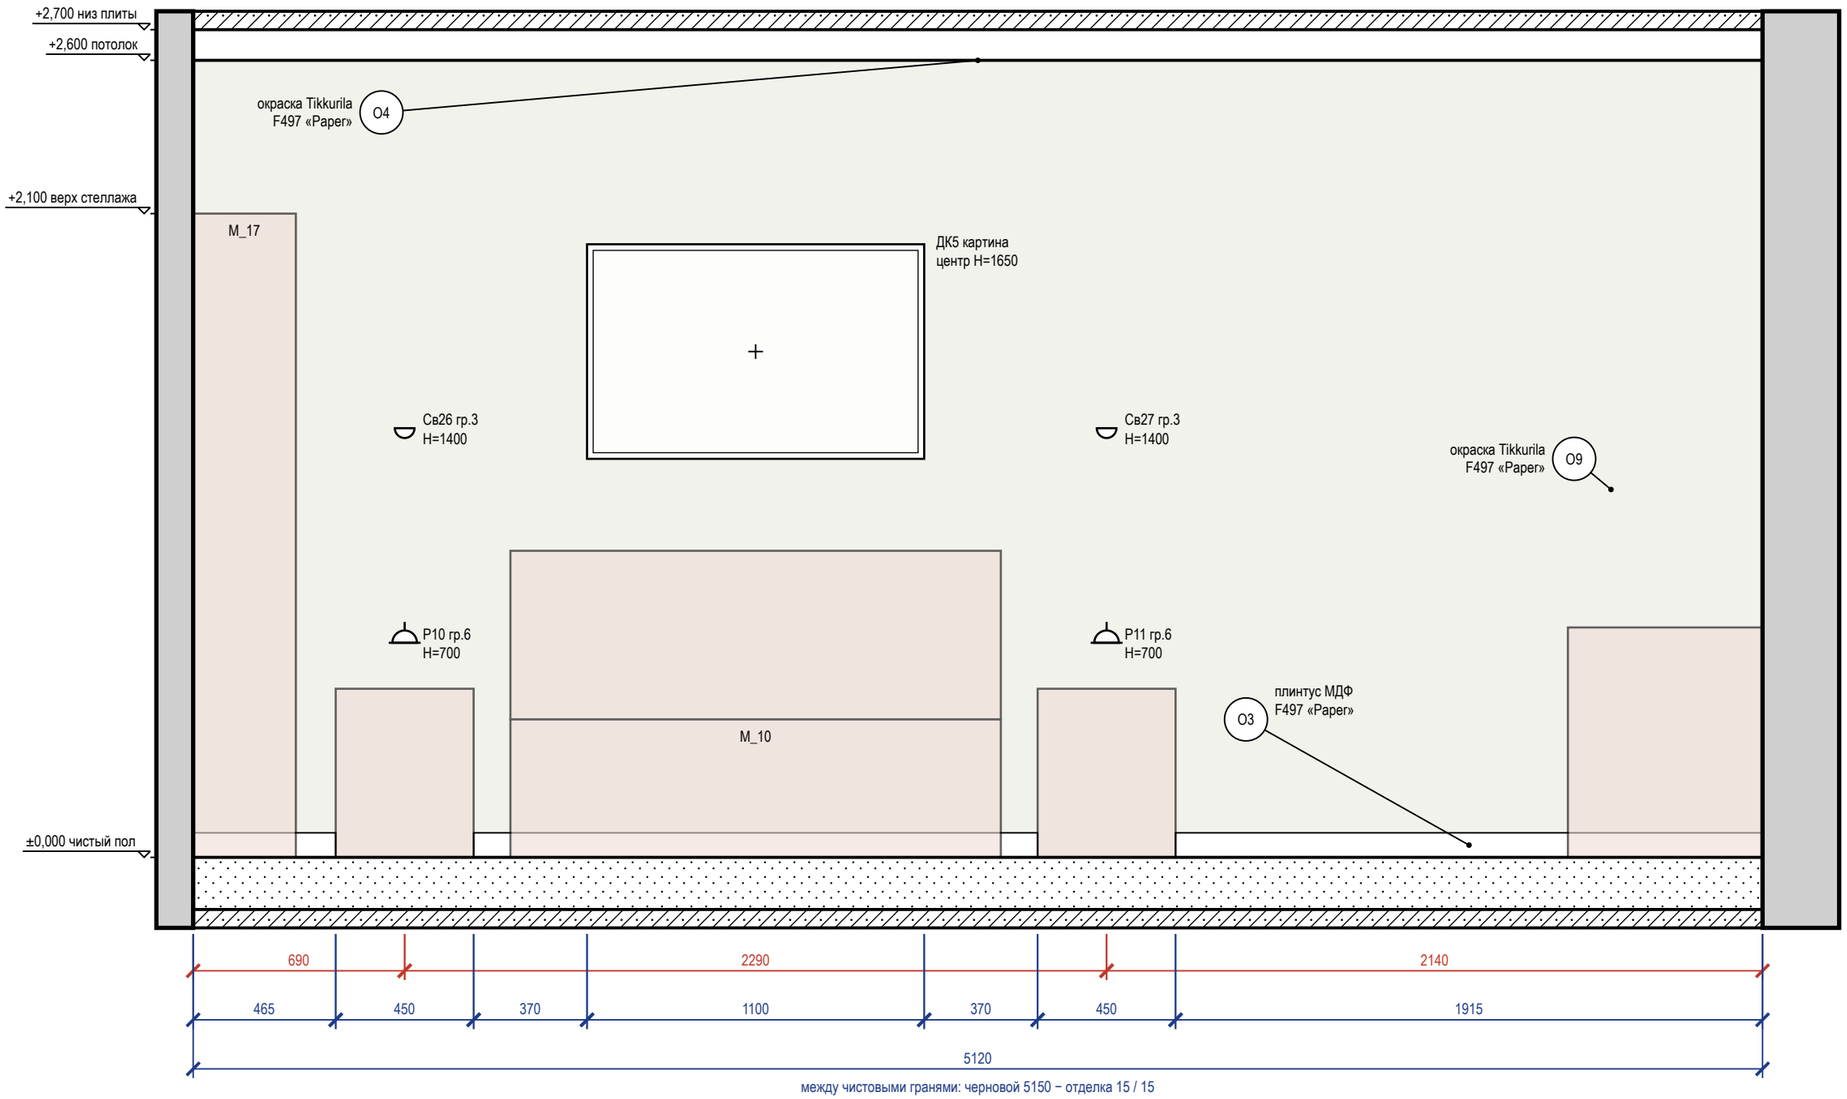


### Схема развёрток (М 1:100)

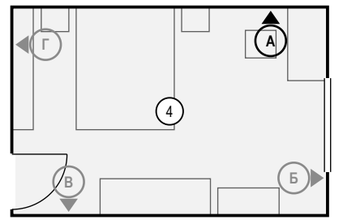


### Ведомость отделки (на листе)

| Марка | Поверхность | Материал, изделие | Цвет, код | Кол. |
|---|---|---|---|---|
| О3 | плинтус | плинтус МДФ, h 80 мм, аналог: плинтус МДФ под окраску 80×16 мм, полуглянцевая | Tikkurila F497 «Paper» | 4,2 м |
| О4 | потолок | окраска, Tikkurila Anti-Reflex 2, глубокоматовая, подготовка Q3 | Tikkurila F497 «Paper» | 17,5 м² |
| О9 | стены | окраска, Tikkurila Joker, шелковисто-матовая, подготовка К3 | Tikkurila F497 «Paper» | 13,3 м² |

### Примечания

1. Размеры — в мм от чистовых поверхностей стен; условные обозначения и общие указания — лист 3.
2. Картины и зеркала крепить к основанию по паспорту изделия (закладные и анкеры — в перечне скрытых работ); крест — ось центра предмета.

| | | | | |
|---|---|---|---|---|
| | Лист | № док. | Подпись | Дата |
| Дизайнер | Кырлан А.С. | | | 04.11.26 |


Проект: Четырёхкомнатная квартира — М 1:20

Развёртка стены А. Детская 1 (пом. 4)


| Стадия | Лист | Листов |
|---|---|---|
| П | 63 | 120 |

выпуск 04.11.2026 № b23f08ad9b · стр. 63 из 120

## Развёртка стены Б

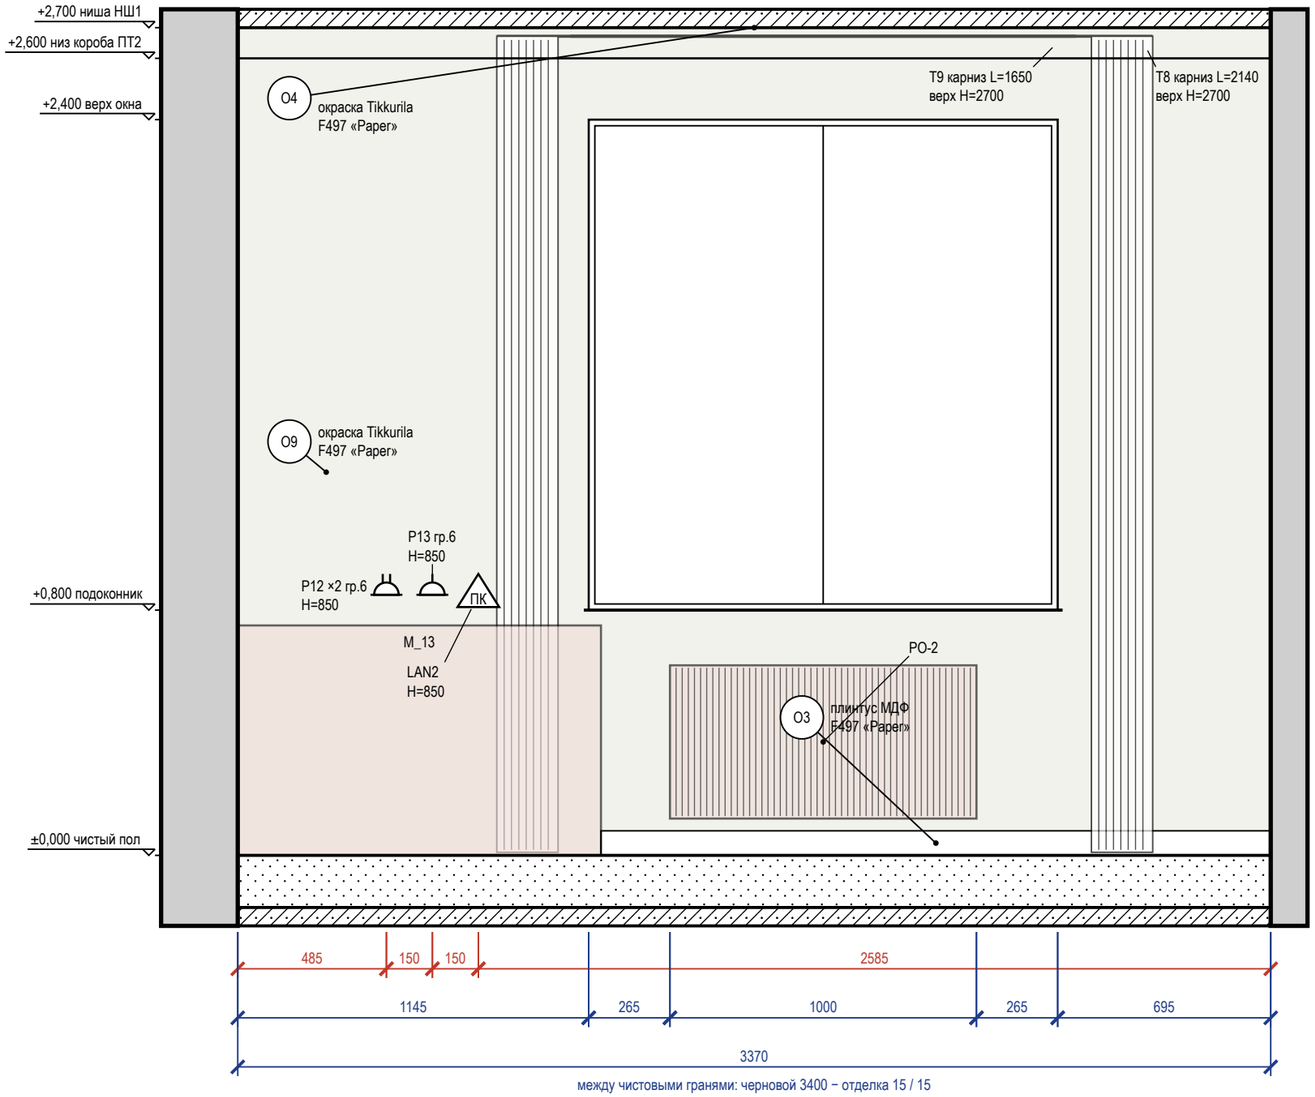


### Схема развёрток (М 1:100)

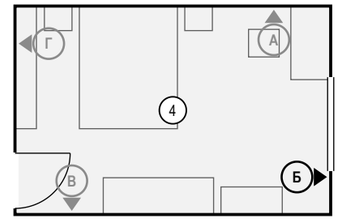


### Ведомость отделки (на листе)

| Марка | Поверхность | Материал, изделие | Цвет, код | Кол. |
|---|---|---|---|---|
| О3 | плинтус | плинтус МДФ, h 80 мм, аналог: плинтус МДФ под окраску 80×16 мм, полуглянцевая | Tikkurila F497 «Paper» | 2,2 м |
| О4 | потолок | окраска, Tikkurila Anti-Reflex 2, глубокоматовая, подготовка Q3 | Tikkurila F497 «Paper» | 17,5 м² |
| О9 | стены | окраска, Tikkurila Joker, шелковисто-матовая, подготовка К3 | Tikkurila F497 «Paper» | 6,7 м² |


### Примечания

1. Размеры — в мм от чистовых поверхностей стен; условные обозначения и общие указания — лист 3.
2. Карнизы (шины) — по ведомости текстиля декоратора: длина L и верх H на развёртке — те же числа, что в ведомости; крепление — до окраски потолка.


| | | | | | | |
|---|---|---|---|---|---|---|
| | | | | | Проект: Четырёхкомнатная квартира | М 1:20 |
| | Лист | № док. | Подпись | Дата | | |
| Дизайнер | Кырлан А.С. | | | 04.11.26 | Развёртка стены Б. Детская 1 (пом. 4) | |

| Стадия | Лист | Листов |
|---|---|---|
| П | 64 | 120 |

## Развёртка стены В

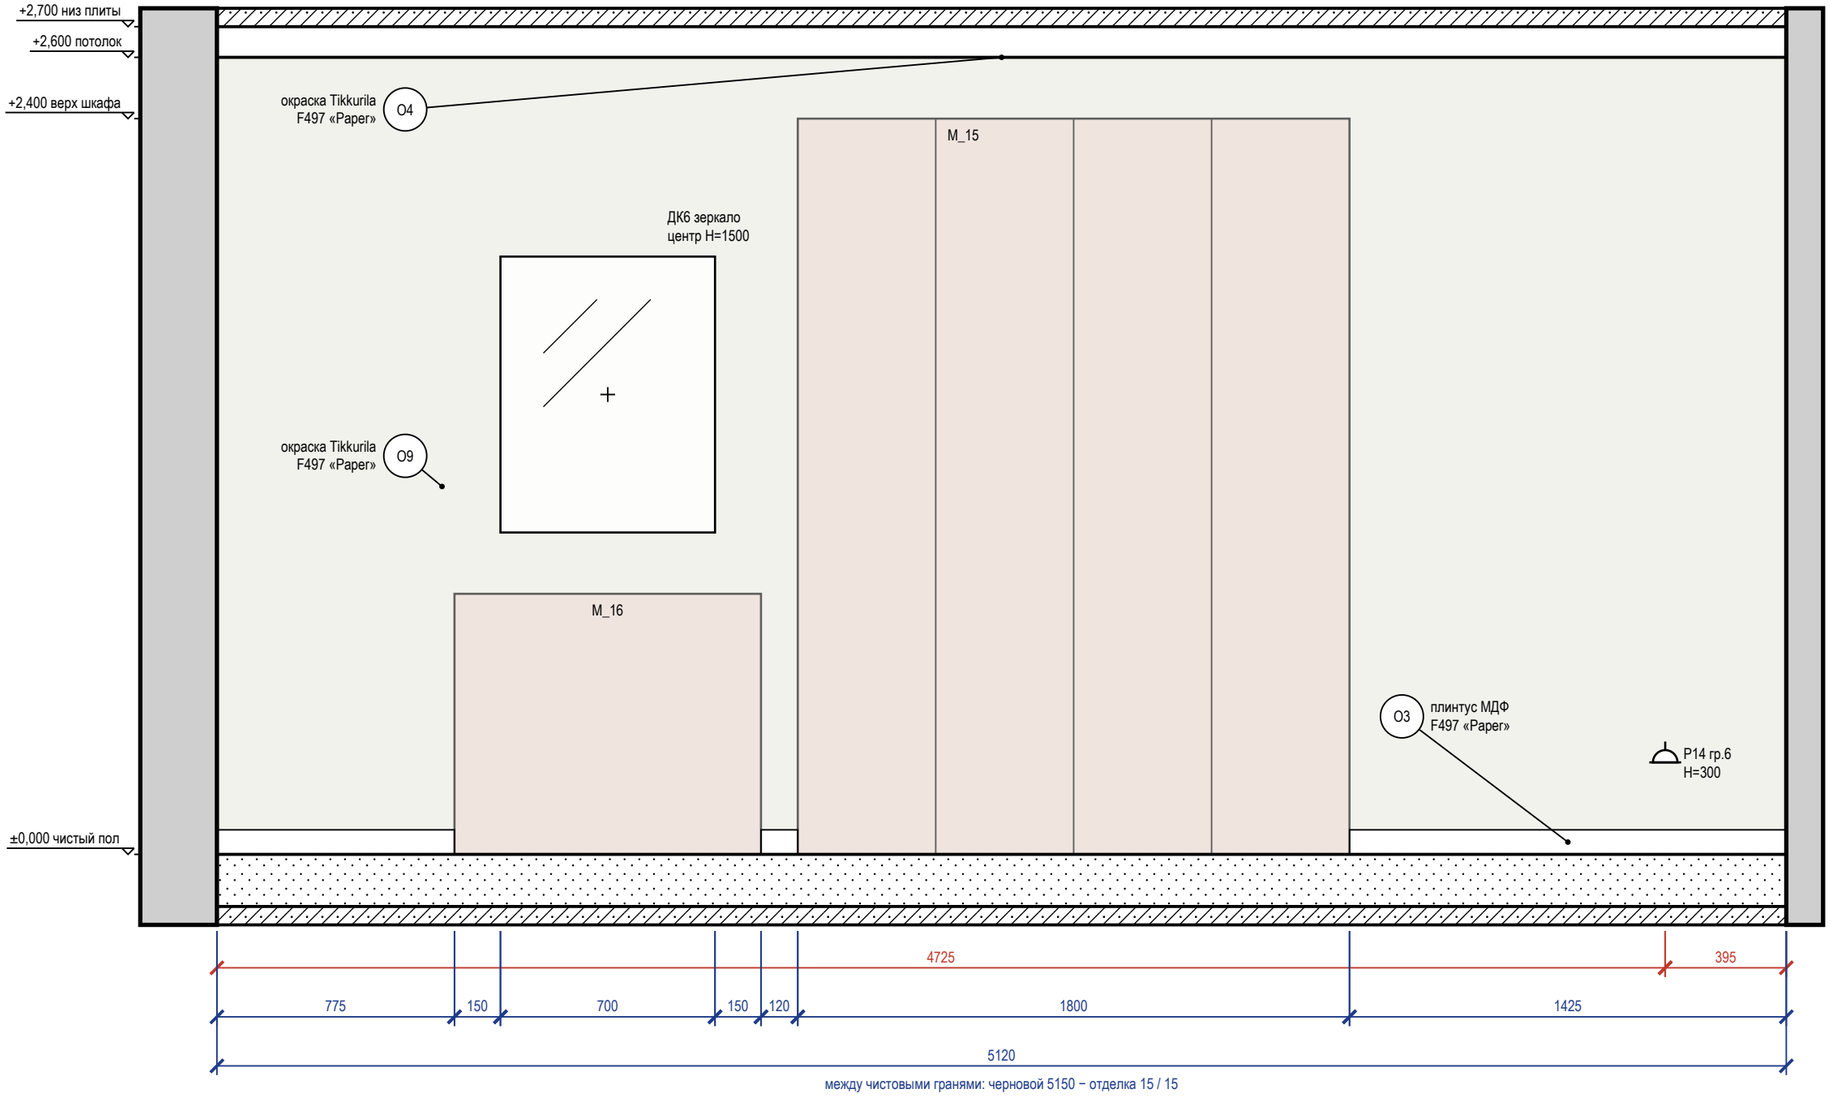


### Схема развёрток (М 1:100)

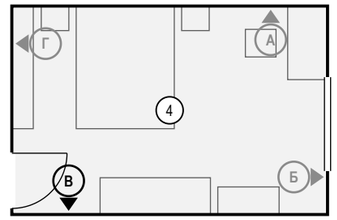


### Ведомость отделки (на листе)

| Марка | Поверхность | Материал, изделие | Цвет, код | Кол. |
|---|---|---|---|---|
| О3 | плинтус | плинтус МДФ, h 80 мм, аналог: плинтус МДФ под окраску 80×16 мм, полуглянцевая | Tikkurila F497 «Paper» | 2,3 м |
| О4 | потолок | окраска, Tikkurila Anti-Reflex 2, глубокоматовая, подготовка Q3 | Tikkurila F497 «Paper» | 17,5 м² |
| О9 | стены | окраска, Tikkurila Joker, шелковисто-матовая, подготовка К3 | Tikkurila F497 «Paper» | 13,3 м² |

### Примечания

1. Размеры — в мм от чистовых поверхностей стен; условные обозначения и общие указания — лист 3.
2. Картины и зеркала крепить к основанию по паспорту изделия (закладные и анкеры — в перечне скрытых работ); крест — ось центра предмета.


| | | | | |
|---|---|---|---|---|
| | Лист | № док. | Подпись | Дата |
| Дизайнер | Кырлан А.С. | | | 04.11.26 |

Проект: Четырёхкомнатная квартира — М 1:20

Развёртка стены В. Детская 1 (пом. 4)


| Стадия | Лист | Листов |
|---|---|---|
| П | 65 | 120 |

## Развёртка стены Г

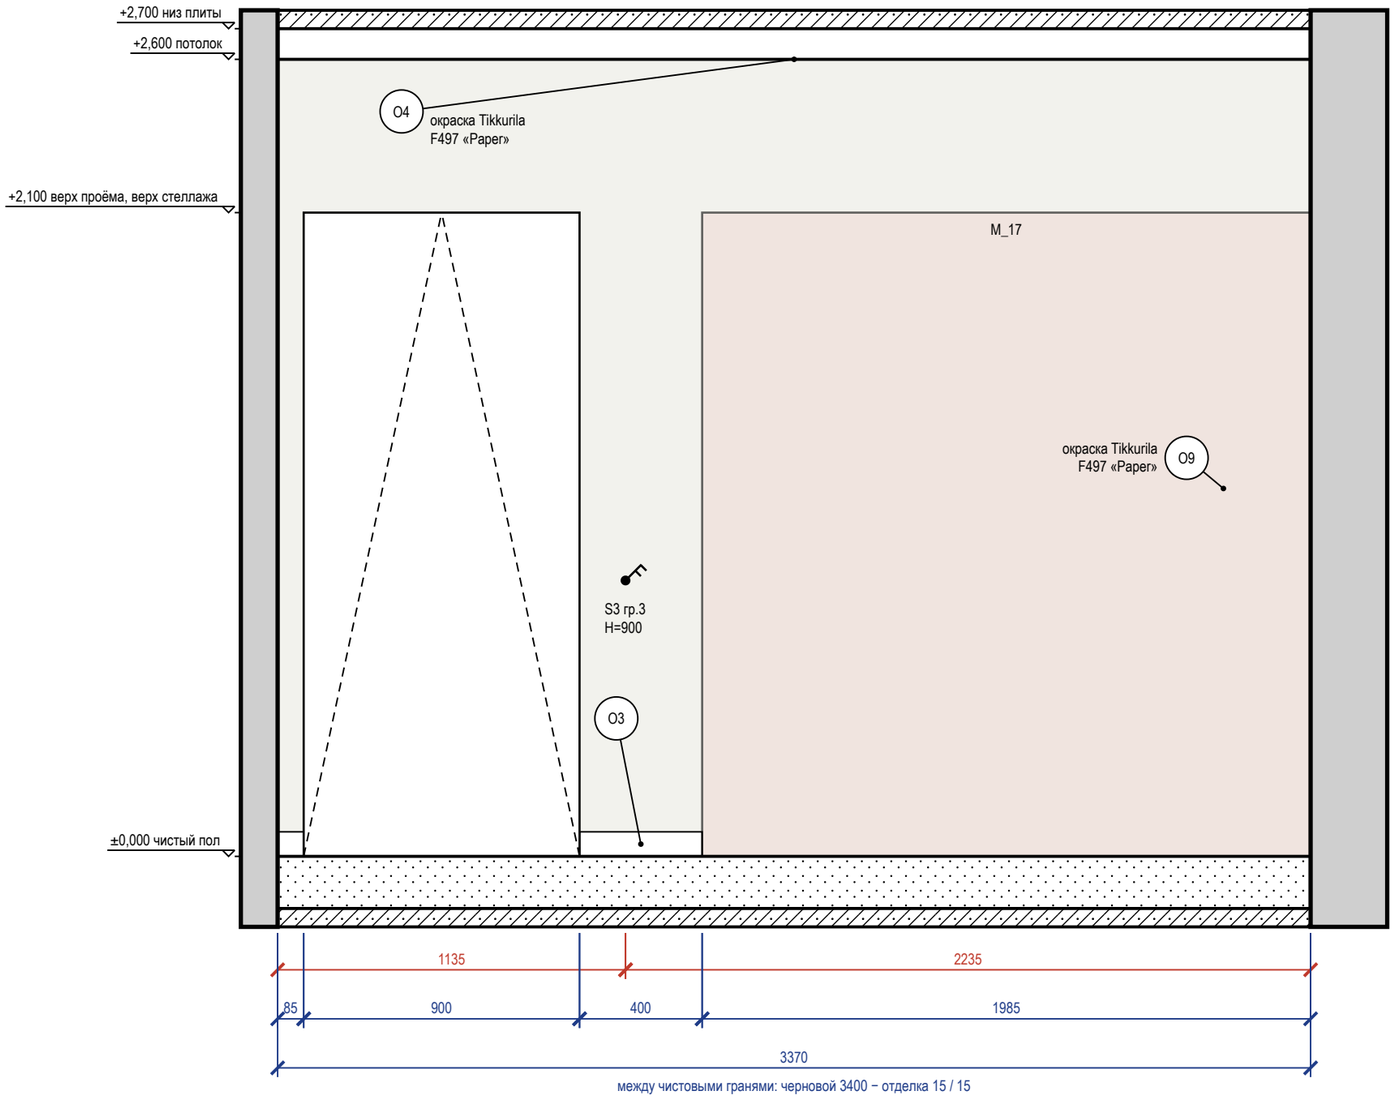


между чистовыми гранями: черновой 3400 − отделка 15 / 15

### Схема развёрток (М 1:100)

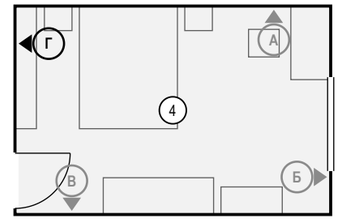


### Ведомость отделки (на листе)


| Марка | Поверхность | Материал, изделие | Цвет, код | Кол. |
|---|---|---|---|---|
| О3 | плинтус | плинтус МДФ, h 80 мм, аналог: плинтус МДФ под окраску 80×16 мм, полуглянцевая | Tikkurila F497 «Paper» | 0,5 м |
| О4 | потолок | окраска, Tikkurila Anti-Reflex 2, глубокоматовая, подготовка Q3 | Tikkurila F497 «Paper» | 17,5 м² |
| О9 | стены | окраска, Tikkurila Joker, шелковисто-матовая, подготовка К3 | Tikkurila F497 «Paper» | 6,9 м² |

### Примечания

1. Размеры — в мм от чистовых поверхностей стен; условные обозначения и общие указания — лист 3.


| | | | | | | |
|---|---|---|---|---|---|---|
| | | | | | Проект: Четырёхкомнатная квартира | М 1:20 |
| | Лист | № док. | Подпись | Дата | | |
| Дизайнер | Кырлан А.С. | | | 04.11.26 | Развёртка стены Г. Детская 1 (пом. 4) | Стадия: П; Лист: 66; Листов: 120 |

## Развёртка стены А

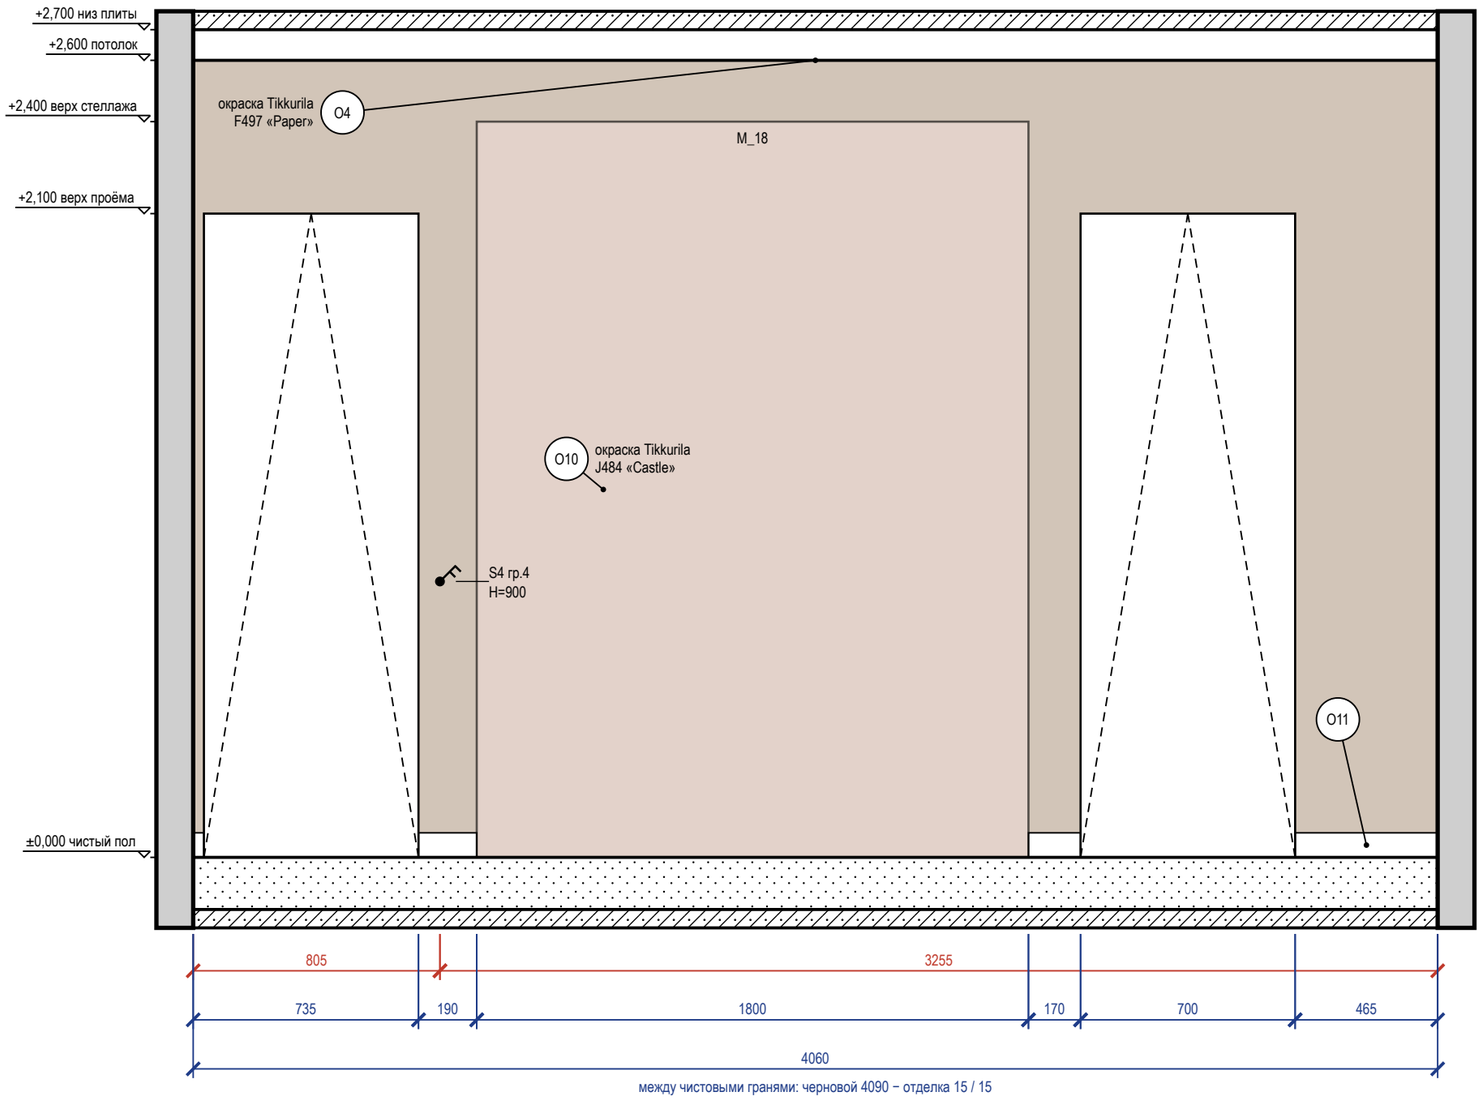



между чистовыми гранями: черновой 4090 − отделка 15 / 15

## Развёртка стены Б

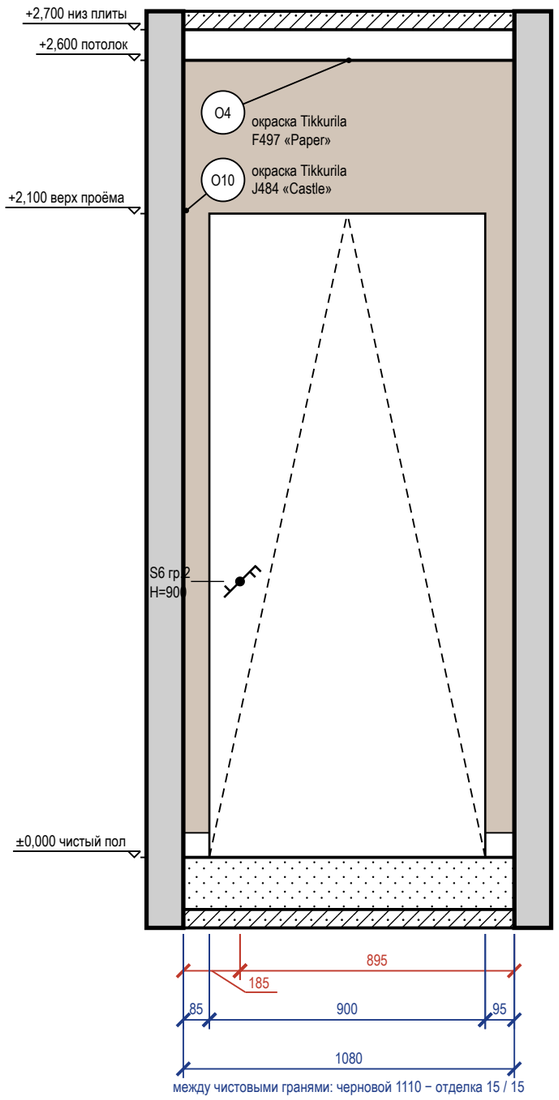


между чистовыми гранями: черновой 1110 − отделка 15 / 15

### Схема развёрток (М 1:100)

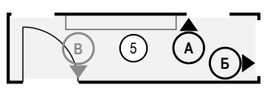


### Ведомость отделки (на листе)

| Марка | Поверхность | Материал, изделие | Цвет, код | Кол. |
|---|---|---|---|---|
| O4 | потолок | окраска, Tikkurila Anti-Reflex 2, глубокоматовая, подготовка Q3 | Tikkurila F497 «Paper» | 4,5 м² |
| O10 | стены | окраска, Tikkurila Optiva 20 Semimatt, шелковисто-матовая, подготовка К3 | Tikkurila J484 «Castle» | 8,5 м² |
| O11 | плинтус | плинтус МДФ, h 80 мм, аналог: плинтус МДФ под окраску 80×16 мм, полуглянцевая | Tikkurila J484 «Castle» | 1 м |


### Примечания

1. Размеры — в мм от чистовых поверхностей стен; условные обозначения и общие указания — лист 3.

| | | | | | |
|---|---|---|---|---|---|
| | | | | | Проект: Четырёхкомнатная квартира — М 1:20 |
| | Лист | № док. | Подпись | Дата | |
| Дизайнер | Кырлан А.С. | | | 04.11.26 | Развёртки стен А, Б. Коридор (пом. 5) |
| | | | | | Стадия: П; Лист: 67; Листов: 120 |

выпуск 04.11.2026 № b23f08ad9b · стр. 67 из 120

## Развёртка стены В

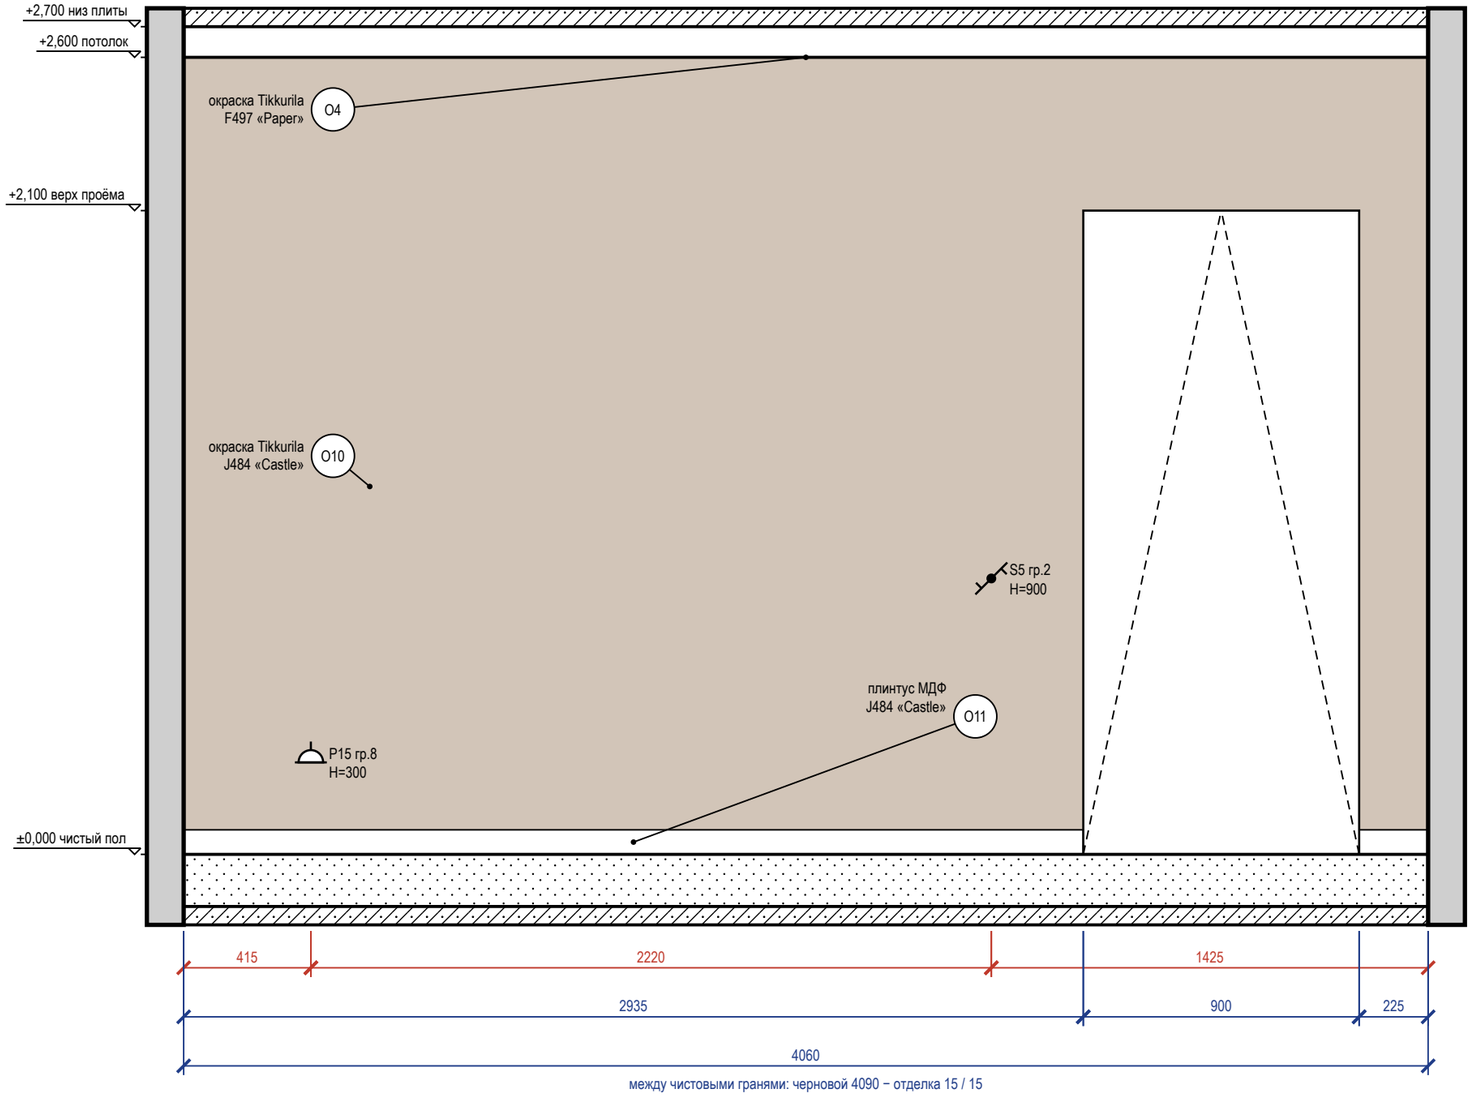


### Схема развёрток (М 1:100)





### Ведомость отделки (на листе)

| Марка | Поверхность | Материал, изделие | Цвет, код | Кол. |
|---|---|---|---|---|
| O4 | потолок | окраска, Tikkurila Anti-Reflex 2, глубокоматовая, подготовка Q3 | Tikkurila F497 «Paper» | 4,5 м² |
| O10 | стены | окраска, Tikkurila Optiva 20 Semimatt, шелковисто-матовая, подготовка К3 | Tikkurila J484 «Castle» | 8,7 м² |
| O11 | плинтус | плинтус МДФ, h 80 мм, аналог: плинтус МДФ под окраску 80×16 мм, полуглянцевая | Tikkurila J484 «Castle» | 3,2 м |

**6** **Плинтус МДФ 80×16 мм у окрашенной стены по керамограниту (плитке) (М 1:20)**

Узел 6 — лист С8

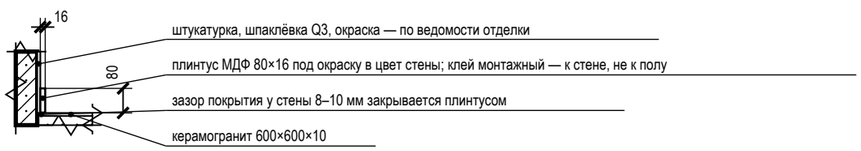



### Примечания


1. Размеры — в мм от чистовых поверхностей стен; условные обозначения и общие указания — лист 3.

| | | | | | |
|---|---|---|---|---|---|
| | | | | | Проект: Четырёхкомнатная квартира — М 1:20 |
| | Лист | № док. | Подпись | Дата | |
| Дизайнер | Кырлан А.С. | | | 04.11.26 | Развёртка стены В. Коридор (пом. 5) |
| | | | | | Стадия: П; Лист: 68; Листов: 120 |

## Развёртка стены А

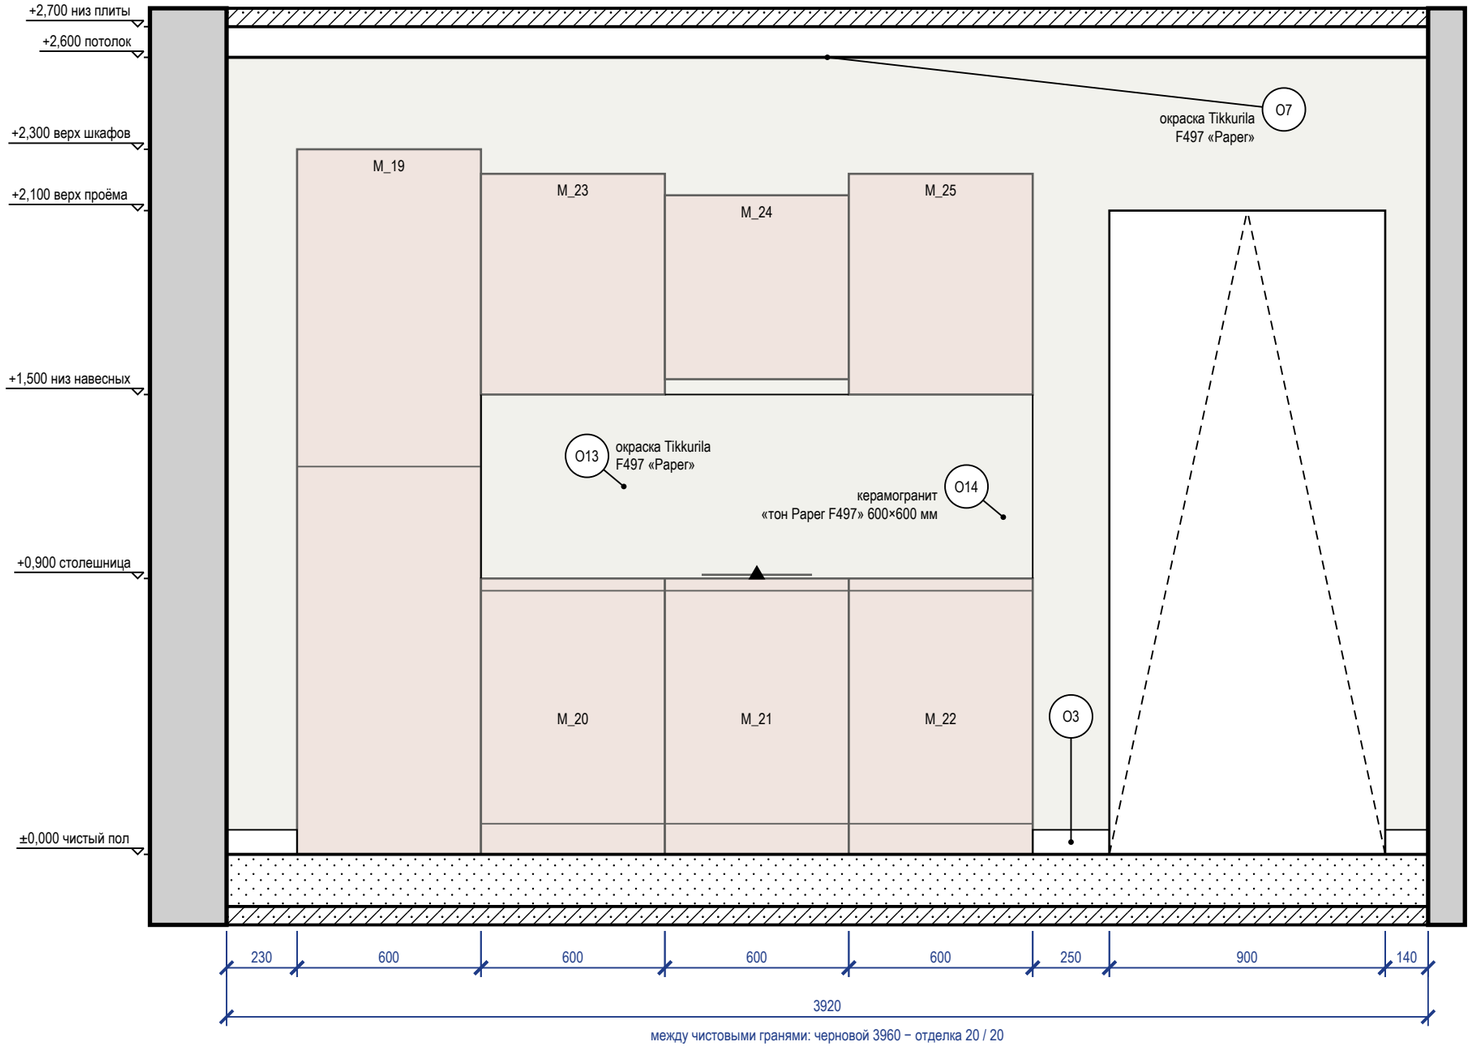


### Схема развёрток (М 1:100)

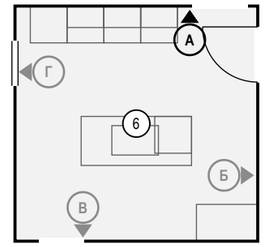


### Ведомость отделки (на листе)


| Марка | Поверхность | Материал, изделие | Цвет, код | Кол. |
|---|---|---|---|---|
| О3 | плинтус | плинтус МДФ, h 80 мм, аналог: плинтус МДФ под окраску 80×16 мм, полуглянцевая | Tikkurila F497 «Paper» | 0,6 м |
| О7 | потолок | окраска, Tikkurila Luja 7, матовая, подготовка Q3 | Tikkurila F497 «Paper» | 15,2 м² |
| О13 | стены | окраска, Tikkurila Luja 7, шелковисто-матовая, подготовка К3 | Tikkurila F497 «Paper» | 7,2 м² |
| О14 | фартук | керамогранит, 600×600×9 мм, аналог: керамогранит матовый, тон F497, затирка CG2WA | #F1F1EC «тон Paper F497» | 1,1 м² |

### Примечания

1. Размеры — в мм от чистовых поверхностей стен; условные обозначения и общие указания — лист 3.
2. Стена А показана двумя видами: здесь — архитектурная развёртка (мебель, отделка, проёмы, высоты), электроточки и выводы ВК с привязками и таблицей — на листе 70 («Привязки»).

| | | | | | | |
|---|---|---|---|---|---|---|
| | | | | | Проект: Четырёхкомнатная квартира | М 1:20 |
| | Лист | № док. | Подпись | Дата | | |
| Дизайнер | Кырлан А.С. | | | 04.11.26 | Развёртка стены А. Кухня (пом. 6), кухонный фронт | Стадия: П; Лист: 69; Листов: 120 |

## Развёртка стены А: электроточки и выводы

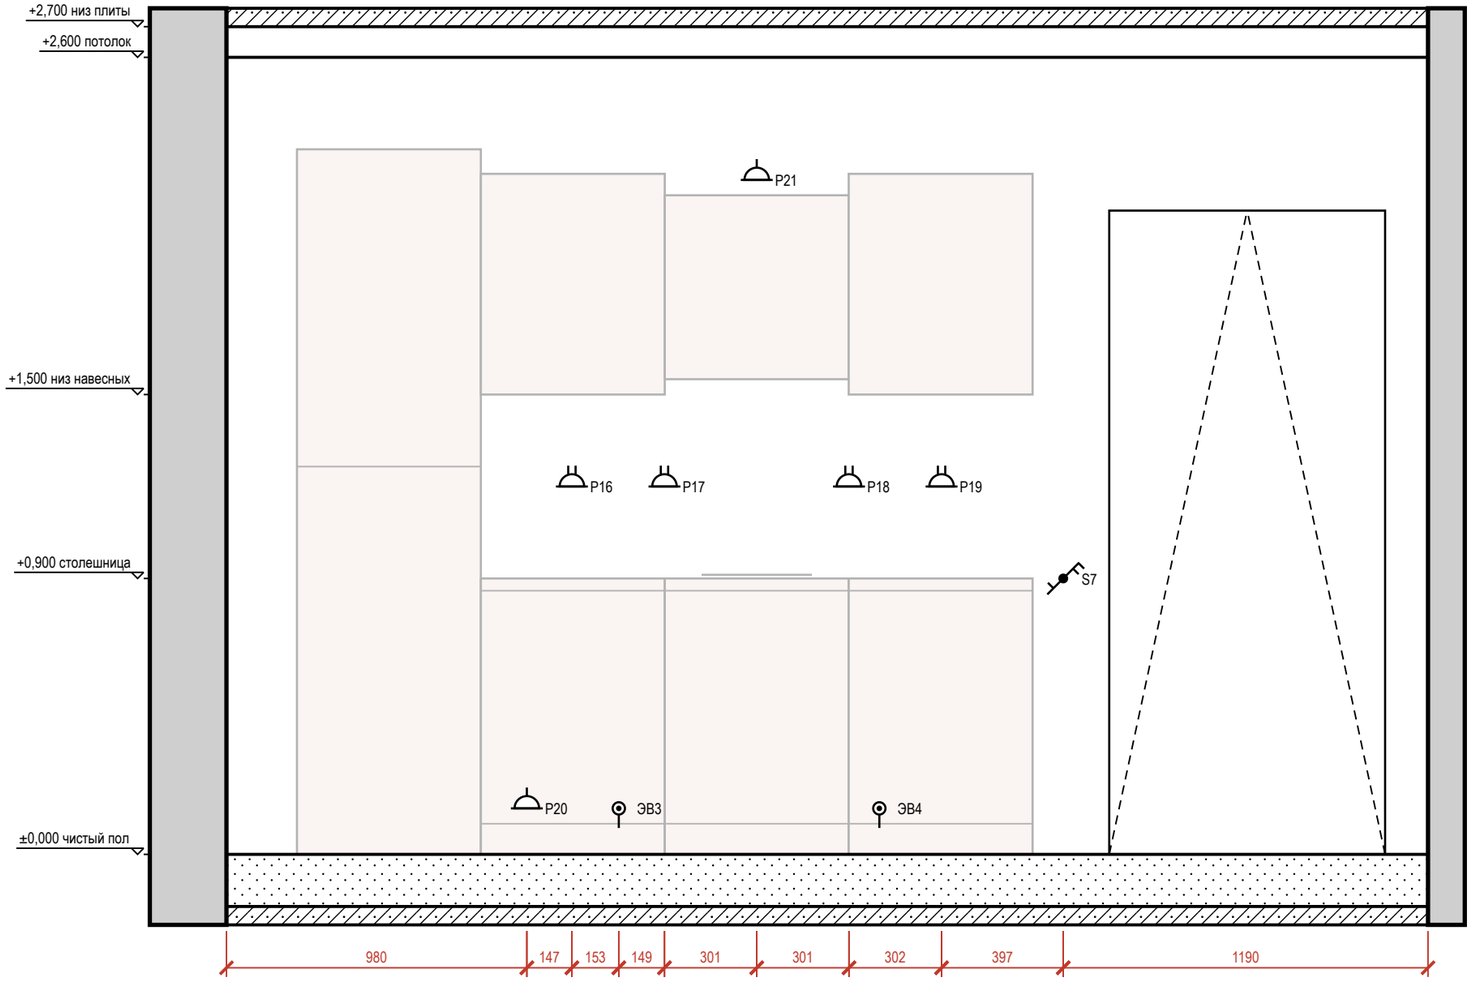



## Таблица привязок электроточек и выводов

| Марка | Назначение | От угла, мм | H от пола, мм | Примечание |
|---|---|---|---|---|
| P20 | розетка: холодильник встроенный M_19 (розетка в модуле M_20) | 980 | 150 | гр. 10 |
| P16 | розетка: фартук: мелкая техника | 1127 | 1200 | рамка 2 поста, гр. 9 |
| ЭВ3 | вывод кабеля: варочная панель M_21 | 1280 | 150 | гр. 11 |
| P17 | розетка: фартук: мелкая техника | 1429 | 1200 | рамка 2 поста, гр. 9 |
| P21 | розетка: вытяжка M_24 (в модуле, съёмная панель) | 1730 | 2200 | гр. 10 |
| P18 | розетка: фартук: мелкая техника | 2031 | 1200 | рамка 2 поста, гр. 9 |
| ЭВ4 | вывод кабеля: духовой шкаф M_21 (вывод в соседнем модуле M_22) | 2130 | 150 | гр. 12 |
| P19 | розетка: фартук: мелкая техника | 2333 | 1200 | рамка 2 поста, гр. 9 |
| S7 | выключатель | 2730 | 900 | гр. 1 |

## Условные обозначения

- розетка с заземляющим контактом; у знака — марка, ×N постов в рамке, гр. — группа щита, H — высота оси, мм
- вывод кабеля для подключения прибора (без розетки), марка ЭВ
- выключатель одноклавишный
- выключатель двухклавишный (флажков — по числу клавиш)
- выключатель с проходной или перекрёстной клавишей (обратный флажок); тип клавиши — в подписи
- привязки точек и выводов от угла и от пола, мм
- марка развёртки: буква стены, стрелка — взгляд

## Схема развёрток (М 1:100)

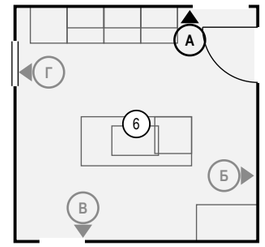



## Примечания

1. Вид «Привязки» стены А — электроточки и выводы ВК; архитектурная развёртка (мебель, отделка, проёмы, высоты) — на листе 69. Мебель и приборы — подложкой для ориентира; их марки и обозначения мебели, проёмов и стен — там же.
2. Привязки — в мм: по горизонтали от левого чистового угла стены до оси изделия, H — от чистого пола до оси; все точки — в таблице привязок. Красная цепочка — привязки по осям; точки ближе 120 мм одна к другой в цепочку не дробятся — их привязки только в таблице.
3. У знака — марка электроточки (P — розетка, S — выключатель, Св — светильник, ЭВ — вывод кабеля); условные обозначения и общие указания — лист 3.


| | | | | | |
|---|---|---|---|---|---|
| | | | | | Проект: Четырёхкомнатная квартира — М 1:20 |
| | Лист | № док. | Подпись | Дата | |
| Дизайнер | Кырлан А.С. | | | 04.11.26 | Привязки электроточек, стена А. Кухня (пом. 6) |

| Стадия | Лист | Листов |
|---|---|---|
| П | 70 | 120 |

## Развёртка стены Б

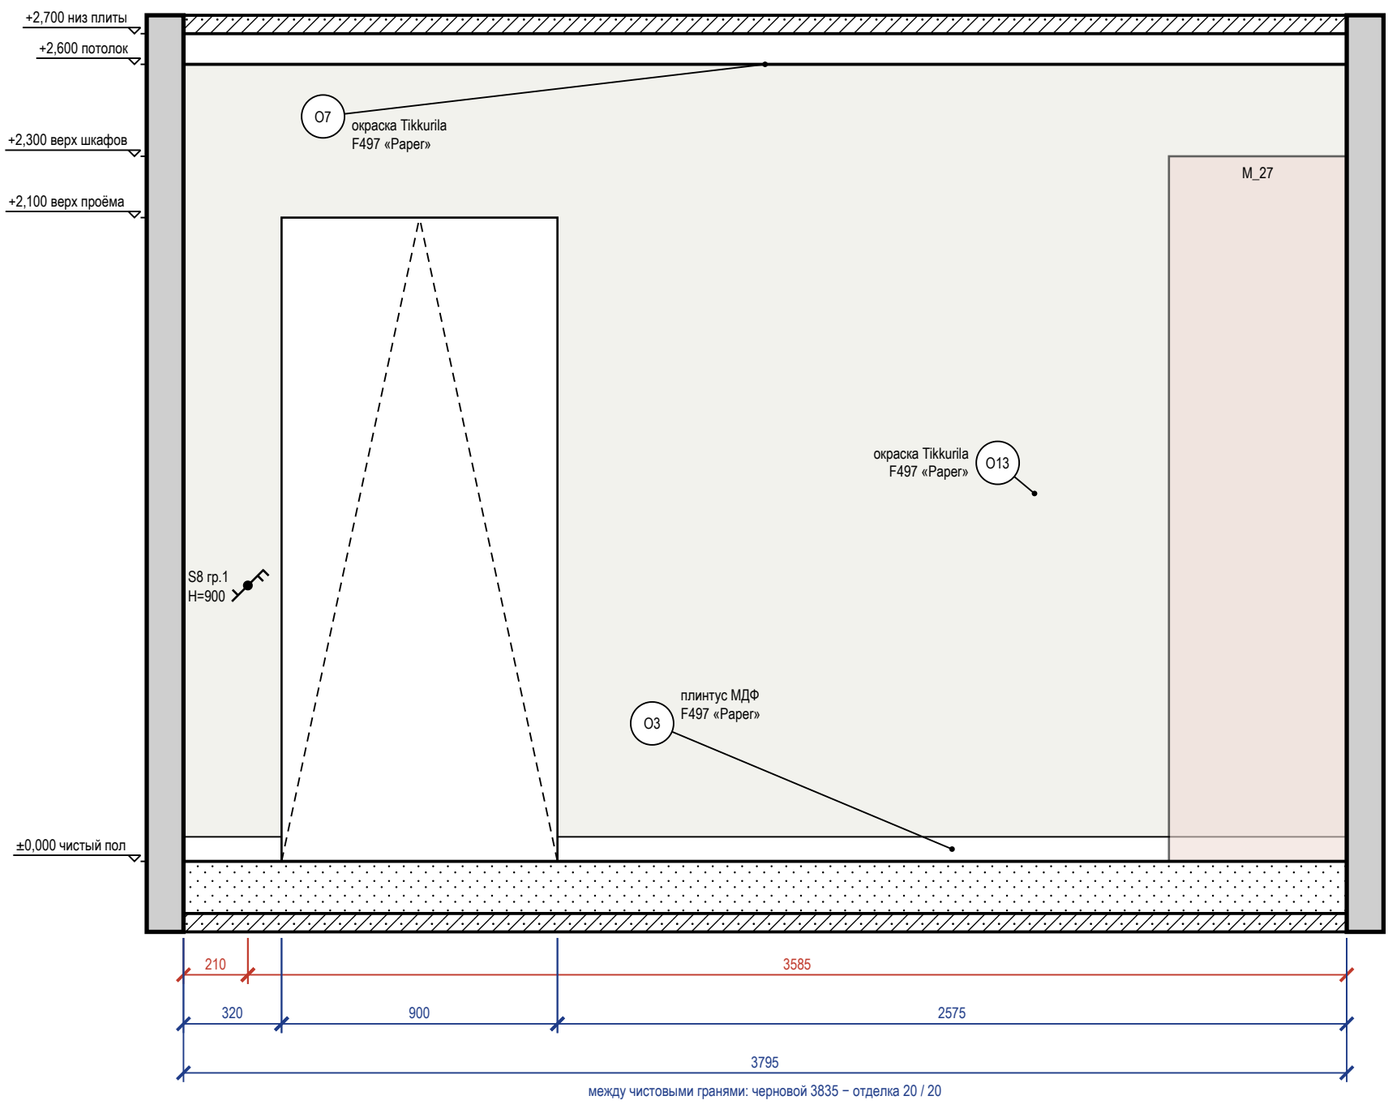


## Схема развёрток (М 1:100)

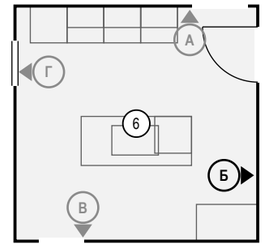


## Ведомость отделки (на листе)


| Марка | Поверхность | Материал, изделие | Цвет, код | Кол. |
|---|---|---|---|---|
| О3 | плинтус | плинтус МДФ, h 80 мм, аналог: плинтус МДФ под окраску 80×16 мм, полуглянцевая | Tikkurila F497 «Paper» | 2,9 м |
| О7 | потолок | окраска, Tikkurila Luja 7, матовая, подготовка Q3 | Tikkurila F497 «Paper» | 15,2 м² |
| О13 | стены | окраска, Tikkurila Luja 7, шелковисто-матовая, подготовка К3 | Tikkurila F497 «Paper» | 8 м² |

## Примечания


1. Размеры — в мм от чистовых поверхностей стен; условные обозначения и общие указания — лист 3.

| | | | | | | | |
|---|---|---|---|---|---|---|---|
| | | | | | Проект: Четырёхкомнатная квартира | | М 1:20 |
| | Лист | № док. | Подпись | Дата | Развёртка стены Б. Кухня (пом. 6) | Стадия | Лист | Листов |
| Дизайнер | Кырлан А.С. | | | 04.11.26 | | П | 71 | 120 |

## Развёртка стены В

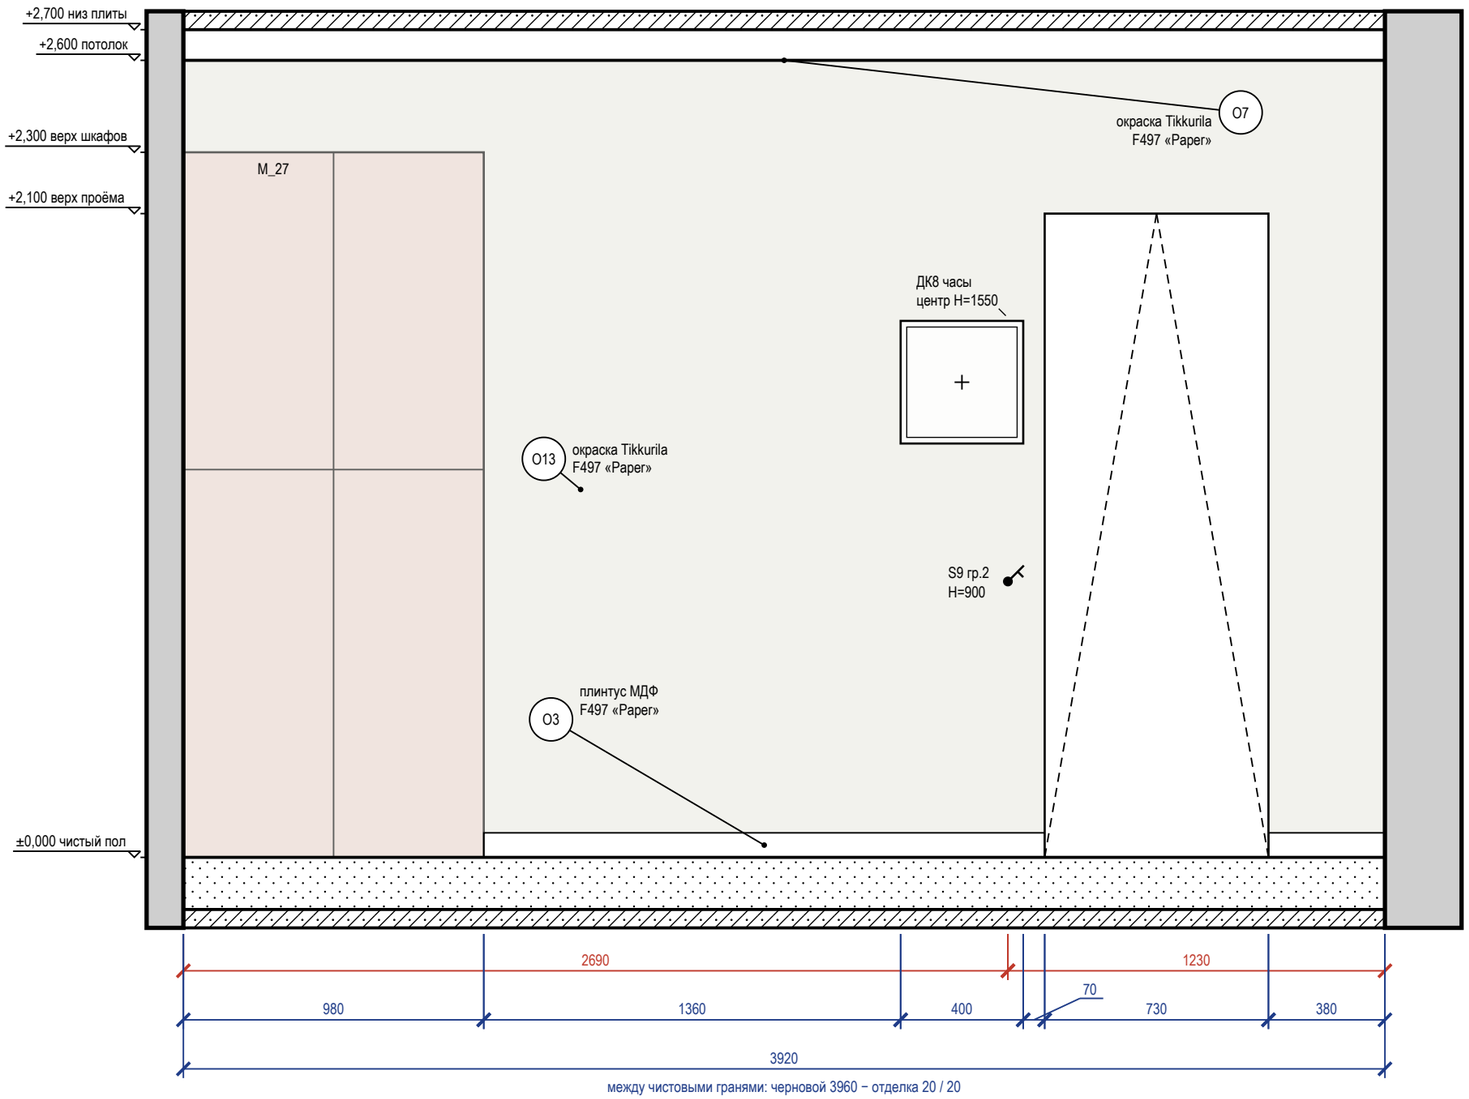


### Схема развёрток (М 1:100)

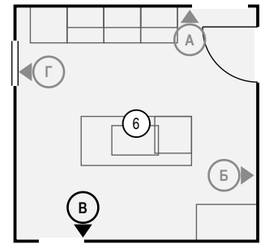


### Ведомость отделки (на листе)


| Марка | Поверхность | Материал, изделие | Цвет, код | Кол. |
|---|---|---|---|---|
| О3 | плинтус | плинтус МДФ, h 80 мм, аналог: плинтус МДФ под окраску 80×16 мм, полуглянцевая | Tikkurila F497 «Paper» | 2,2 м |
| О7 | потолок | окраска, Tikkurila Luja 7, матовая, подготовка Q3 | Tikkurila F497 «Paper» | 15,2 м² |
| О13 | стены | окраска, Tikkurila Luja 7, шелковисто-матовая, подготовка К3 | Tikkurila F497 «Paper» | 8,7 м² |

### Примечания


1. Размеры — в мм от чистовых поверхностей стен; условные обозначения и общие указания — лист 3.
2. Картины и зеркала крепить к основанию по паспорту изделия (закладные и анкеры — в перечне скрытых работ); крест — ось центра предмета.

| | | | | | | |
|---|---|---|---|---|---|---|
| | | | | | Проект: Четырёхкомнатная квартира | М 1:20 |
| | Лист | № док. | Подпись | Дата | Развёртка стены В. Кухня (пом. 6) | Стадия / Лист / Листов |
| Дизайнер | Кырлан А.С. | | | 04.11.26 | | П / 72 / 120 |

## Развёртка стены Г

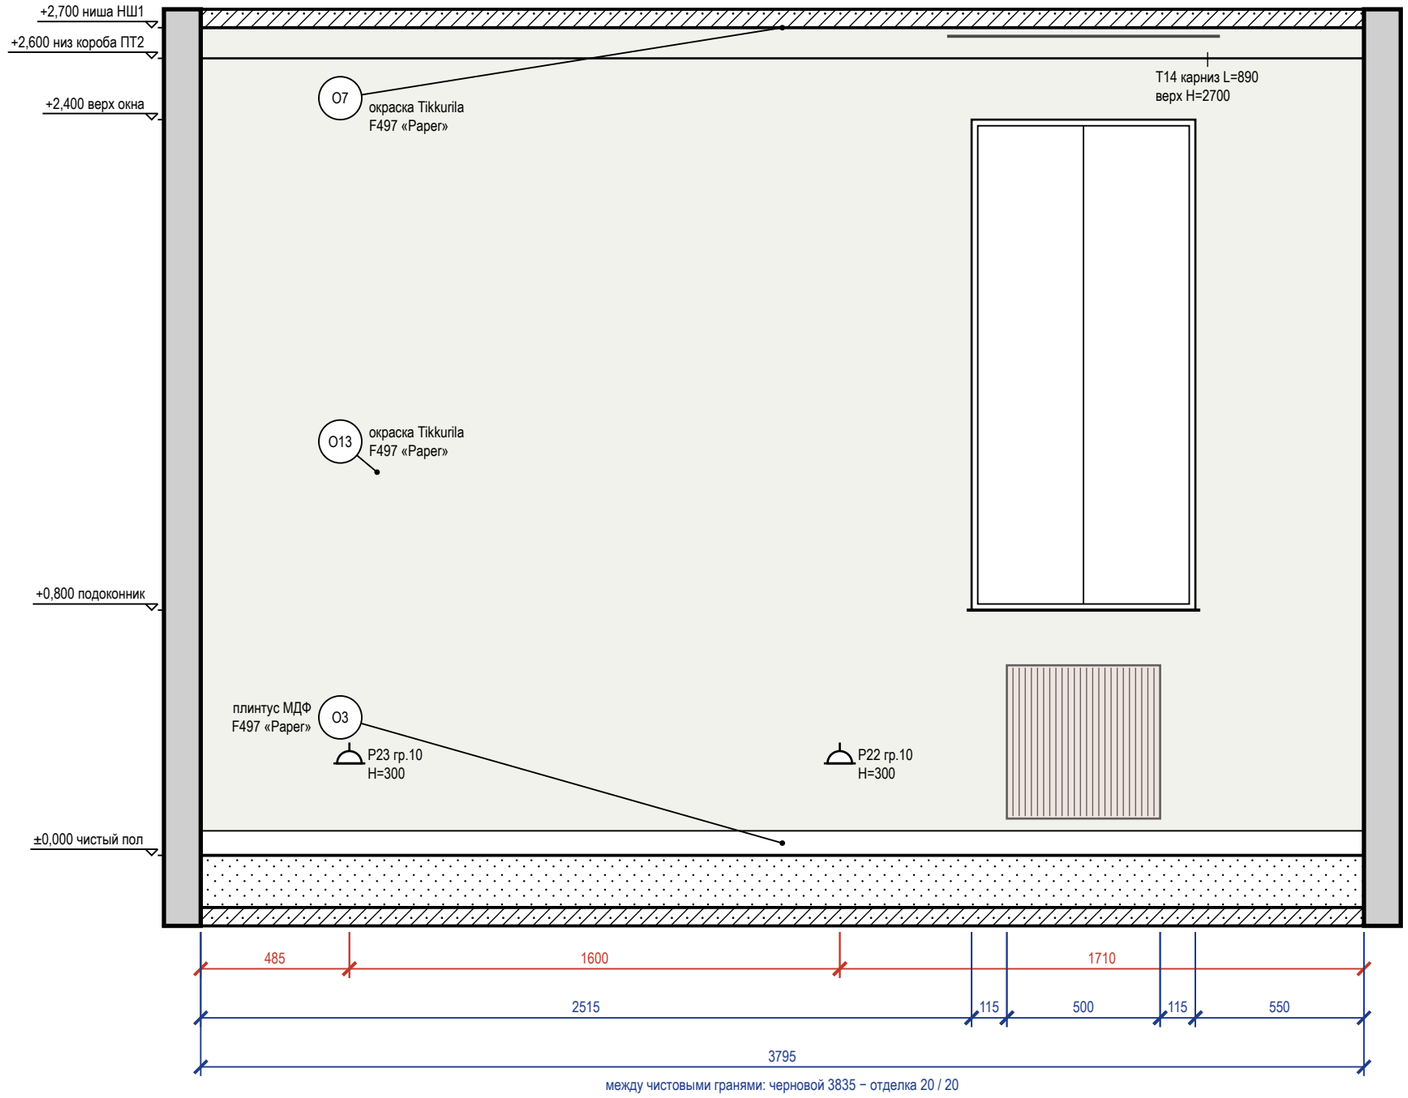


### Схема развёрток (М 1:100)

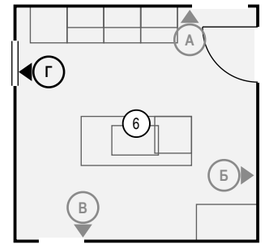


### Ведомость отделки (на листе)


| Марка | Поверхность | Материал, изделие | Цвет, код | Кол. |
|---|---|---|---|---|
| О3 | плинтус | плинтус МДФ, h 80 мм, аналог: плинтус МДФ под окраску 80×16 мм, полуглянцевая | Tikkurila F497 «Paper» | 3,8 м |
| О7 | потолок | окраска, Tikkurila Luja 7, матовая, подготовка Q3 | Tikkurila F497 «Paper» | 15,2 м² |
| О13 | стены | окраска, Tikkurila Luja 7, шелковисто-матовая, подготовка К3 | Tikkurila F497 «Paper» | 9,1 м² |

### Примечания


1. Размеры — в мм от чистовых поверхностей стен; условные обозначения и общие указания — лист 3.
2. Карнизы (шины) — по ведомости текстиля декоратора: длина L и верх H на развёртке — те же числа, что в ведомости; крепление — до окраски потолка.

| | | | | | | |
|---|---|---|---|---|---|---|
| | | | | | Проект: Четырёхкомнатная квартира | М 1:20 |
| | Лист | № док. | Подпись | Дата | Развёртка стены Г. Кухня (пом. 6) | Стадия / Лист / Листов |
| Дизайнер | Кырлан А.С. | | | 04.11.26 | | П / 73 / 120 |


## Развёртка стены А

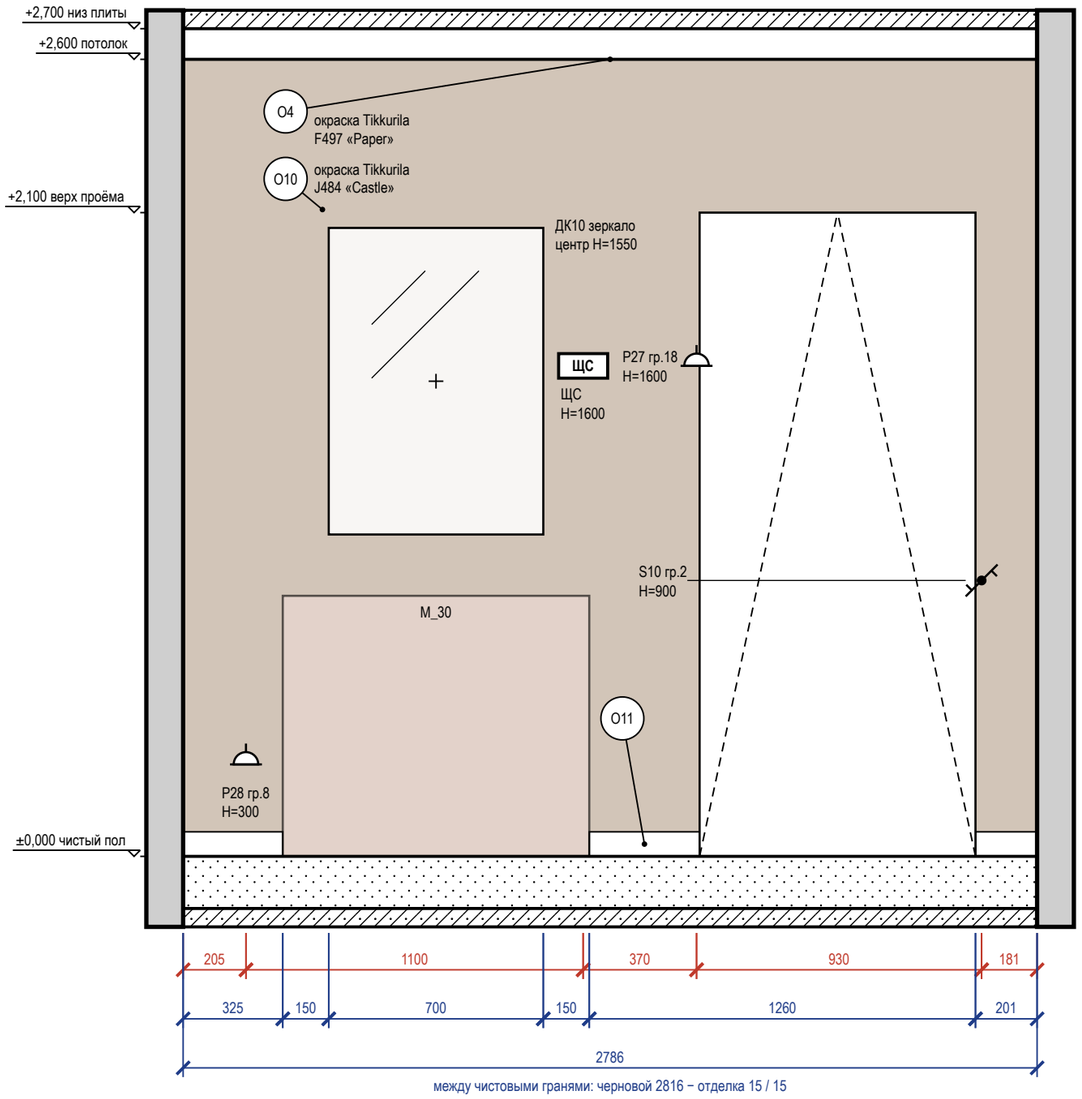


## Развёртка стены Б

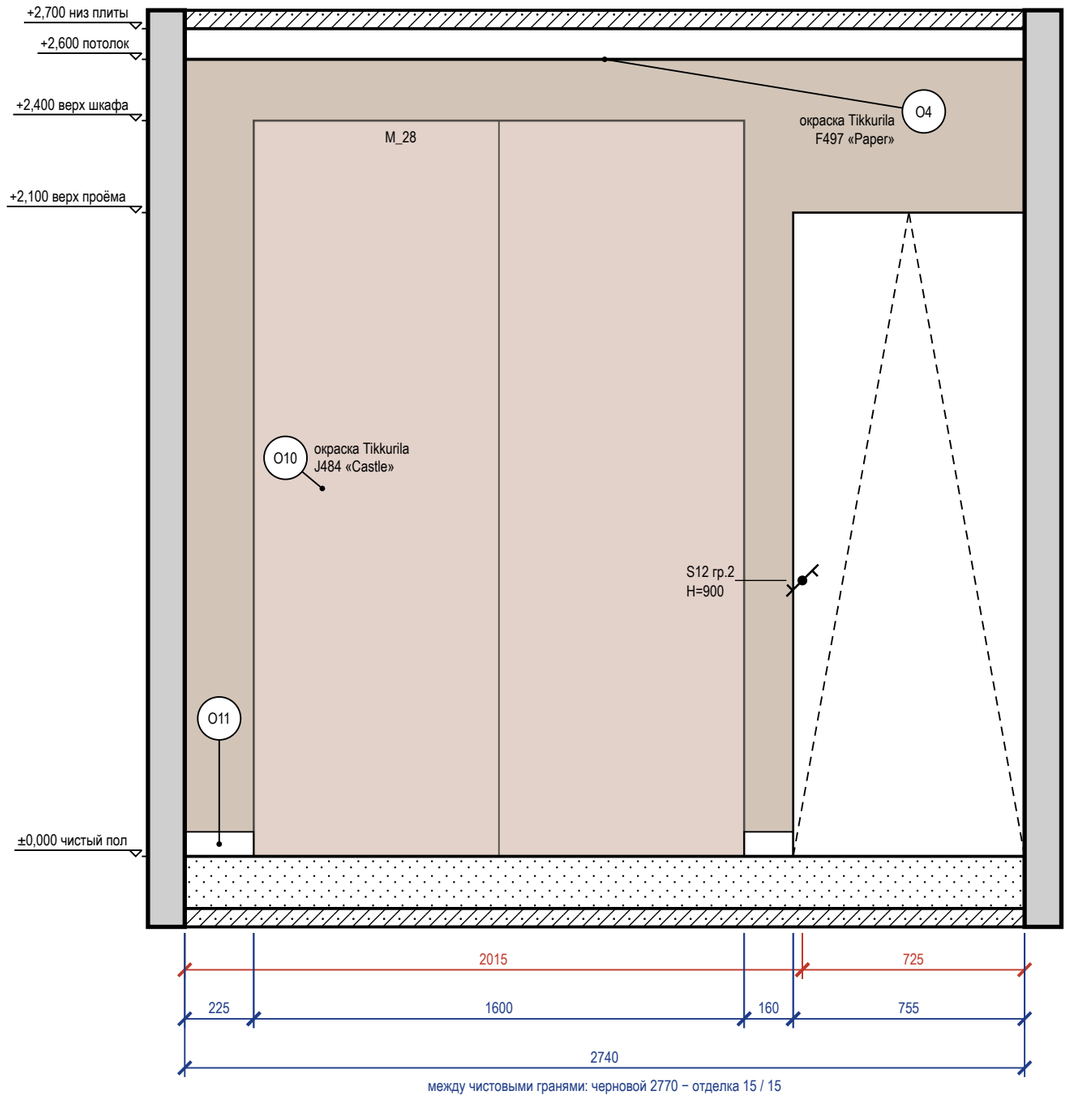


### Схема развёрток (М 1:100)

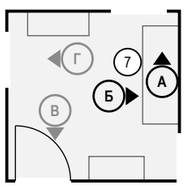


### Ведомость отделки (на листе)

| Марка | Поверхность | Материал, изделие | Цвет, код | Кол. |
|---|---|---|---|---|
| O4 | потолок | окраска, Tikkurila Anti-Reflex 2, глубокоматовая, подготовка Q3 | Tikkurila F497 «Paper» | 7,8 м² |
| O10 | стены | окраска, Tikkurila Optiva 20 Semimatt, шелковисто-матовая, подготовка K3 | Tikkurila J484 «Castle» | 10,9 м² |
| O11 | плинтус | плинтус МДФ, h 80 мм, аналог: плинтус МДФ под окраску 80×16 мм, полуглянцевая | Tikkurila J484 «Castle» | 1,3 м |

### Примечания

1. Размеры — в мм от чистовых поверхностей стен; условные обозначения и общие указания — лист 3.
2. Картины и зеркала крепить к основанию по паспорту изделия (закладные и анкеры — в перечне скрытых работ); крест — ось центра предмета.
3. Дверь заходит за угол помещения: на развёртке показана видимая часть проёма 770 из 900 мм — проверить привязку двери в модели.


| | | | | |
|---|---|---|---|---|
| | Лист | № док. | Подпись | Дата |
| Дизайнер | Кырлан А.С. | | | 04.11.26 |

Проект: Четырёхкомнатная квартира — **М 1:20**

Развёртки стен А, Б. Прихожая-коридор (пом. 7)


| Стадия | Лист | Листов |
|---|---|---|
| П | 74 | 120 |

## Развёртка стены В

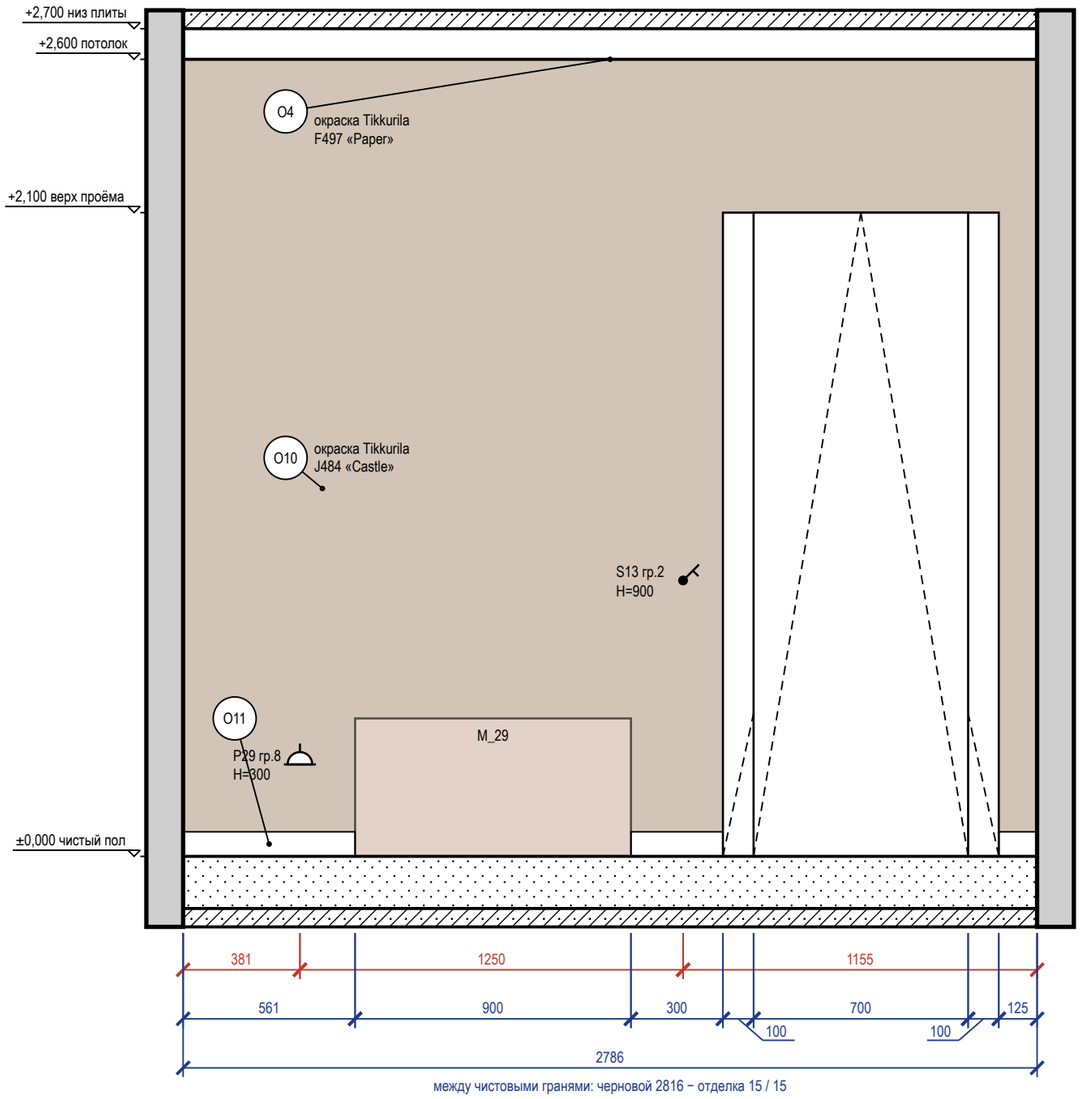



между чистовыми гранями: черновой 2816 − отделка 15 / 15

## Развёртка стены Г

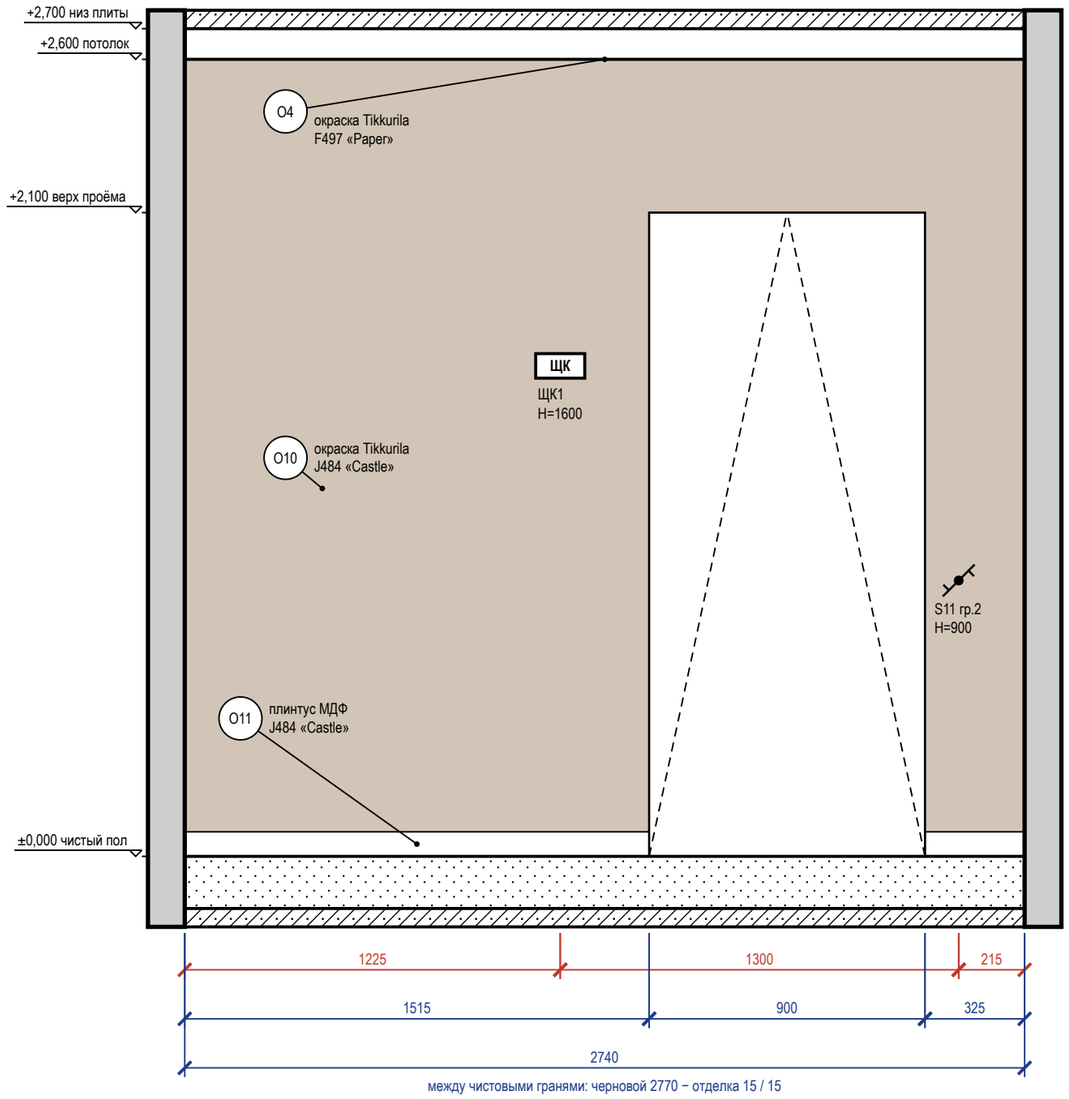


между чистовыми гранями: черновой 2770 − отделка 15 / 15

### Схема развёрток (М 1:100)

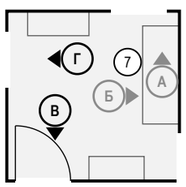


### Ведомость отделки (на листе)


| Марка | Поверхность | Материал, изделие | Цвет, код | Кол. |
|---|---|---|---|---|
| O4 | потолок | окраска, Tikkurila Anti-Reflex 2, глубокоматовая, подготовка Q3 | Tikkurila F497 «Paper» | 7,8 м² |
| O10 | стены | окраска, Tikkurila Optiva 20 Semimatt, шелковисто-матовая, подготовка К3 | Tikkurila J484 «Castle» | 9,1 м² |
| O11 | плинтус | плинтус МДФ, h 80 мм, аналог: плинтус МДФ под окраску 80×16 мм, полуглянцевая | Tikkurila J484 «Castle» | 2,8 м |

### Примечания

1. Размеры — в мм от чистовых поверхностей стен; условные обозначения и общие указания — лист 3.


| | | | | | | |
|---|---|---|---|---|---|---|
| | | | | | Проект: Четырёхкомнатная квартира | М 1:20 |
| | Лист | № док. | Подпись | Дата | Развёртки стен В, Г. Прихожая-коридор (пом. 7) | Стадия / Лист / Листов |
| Дизайнер | Кырлан А.С. | | | 04.11.26 | | П / 75 / 120 |

## Развёртка стены А

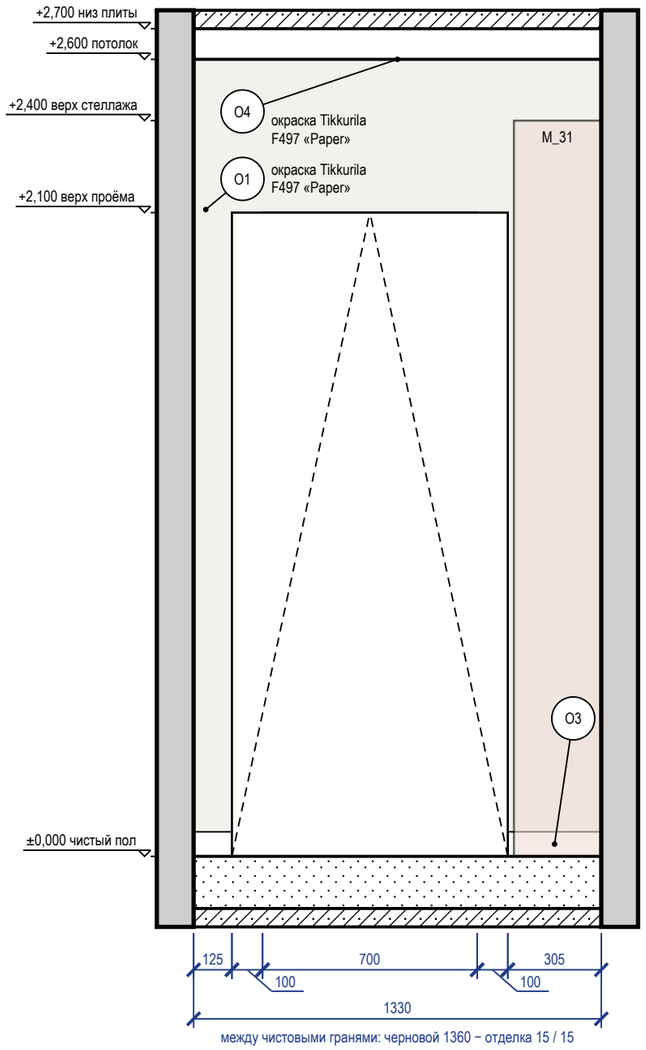



между чистовыми гранями: черновой 1360 − отделка 15 / 15

## Развёртка стены Б

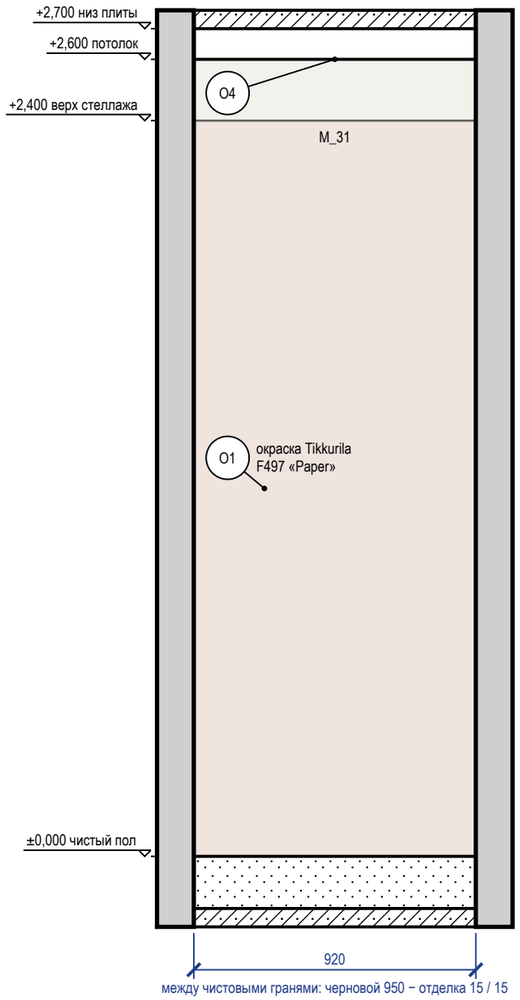


между чистовыми гранями: черновой 950 − отделка 15 / 15

## Развёртка стены В

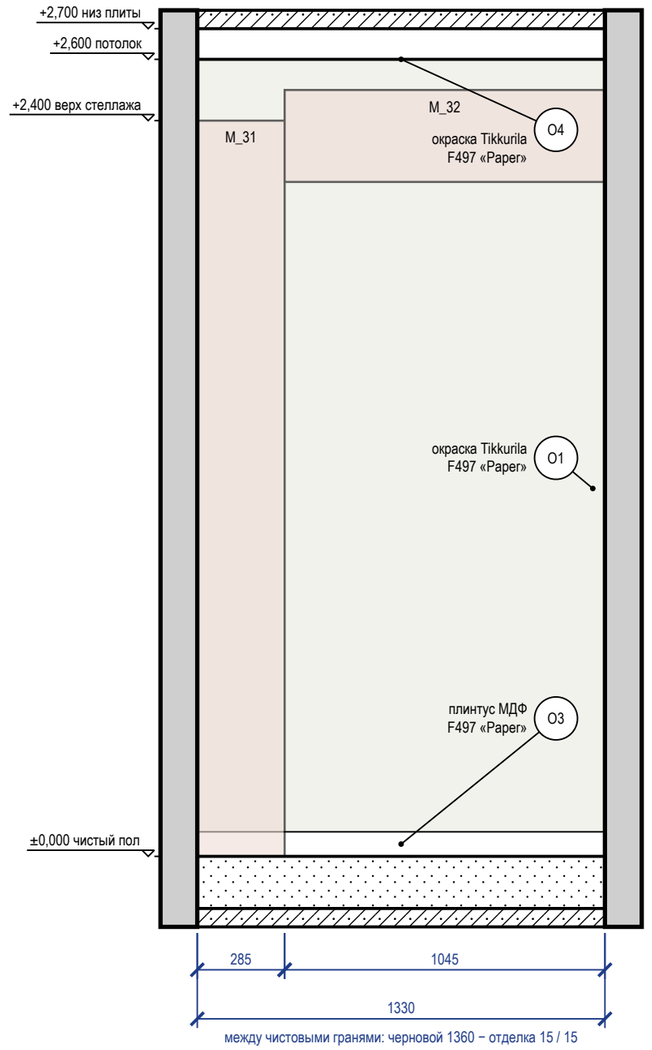


между чистовыми гранями: черновой 1360 − отделка 15 / 15

### Схема развёрток (М 1:100)




### Ведомость отделки (на листе)


| Марка | Поверхность | Материал, изделие | Цвет, код | Кол. |
|---|---|---|---|---|
| O1 | стены | окраска, Tikkurila Optiva 5 Matt, матовая, подготовка К3 | Tikkurila F497 «Paper» | 5,9 м² |
| O3 | плинтус | плинтус МДФ, h 80 мм, аналог: плинтус МДФ под окраску 80×16 мм, полуглянцевая | Tikkurila F497 «Paper» | 1,8 м |
| O4 | потолок | окраска, Tikkurila Anti-Reflex 2, глубокоматовая, подготовка Q3 | Tikkurila F497 «Paper» | 1,3 м² |

### Примечания


1. Размеры — в мм от чистовых поверхностей стен; условные обозначения и общие указания — лист 3.

| | | | | | |
|---|---|---|---|---|---|
| | | | | | Проект: Четырёхкомнатная квартира — М 1:20 |
| | Лист | № док. | Подпись | Дата | Развёртки стен А, Б, В. Гардеробная 2 (пом. 8) |
| Дизайнер | Кырлан А.С. | | | 04.11.26 | Стадия: П · Лист: 76 · Листов: 120 |

## Развёртка стены Г

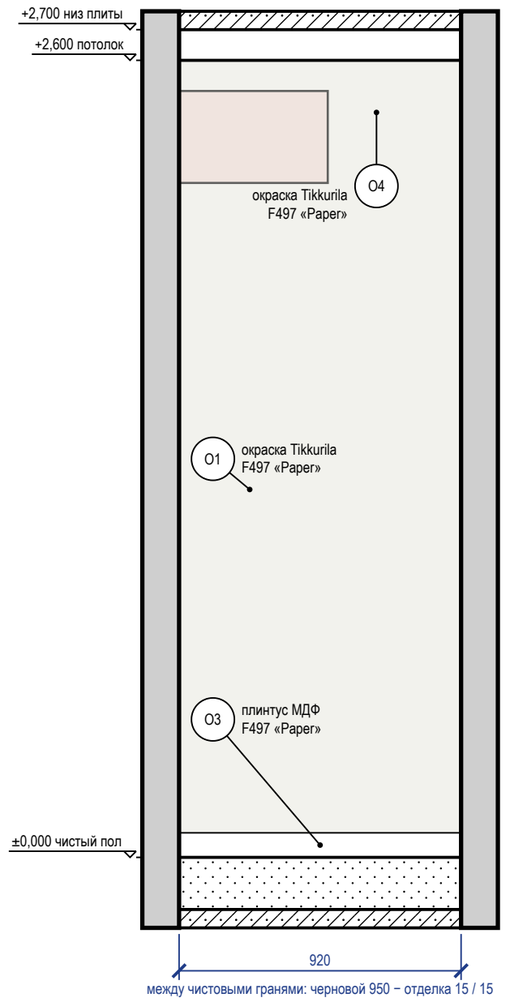


## Схема развёрток (М 1:100)

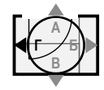


## Ведомость отделки (на листе)


| Марка | Поверхность | Материал, изделие | Цвет, код | Кол. |
|---|---|---|---|---|
| О1 | стены | окраска, Tikkurila Optiva 5 Matt, матовая, подготовка К3 | Tikkurila F497 «Paperг» | 2,4 м² |
| О3 | плинтус | плинтус МДФ, h 80 мм, аналог: плинтус МДФ под окраску 80×16 мм, полуглянцевая | Tikkurila F497 «Paperг» | 0,9 м |
| О4 | потолок | окраска, Tikkurila Anti-Reflex 2, глубокоматовая, подготовка Q3 | Tikkurila F497 «Paperг» | 1,3 м² |

### Примечания


1. Размеры — в мм от чистовых поверхностей стен; условные обозначения и общие указания — лист 3.

| | | | | | | |
|---|---|---|---|---|---|---|
| | | | | | Проект: Четырёхкомнатная квартира | М 1:20 |
| | Лист | № док. | Подпись | Дата | | |
| Дизайнер | Кырлан А.С. | | | 04.11.26 | Развёртка стены Г. Гардеробная 2 (пом. 8) | Стадия: П; Лист: 77; Листов: 120 |

## Развёртка стены А

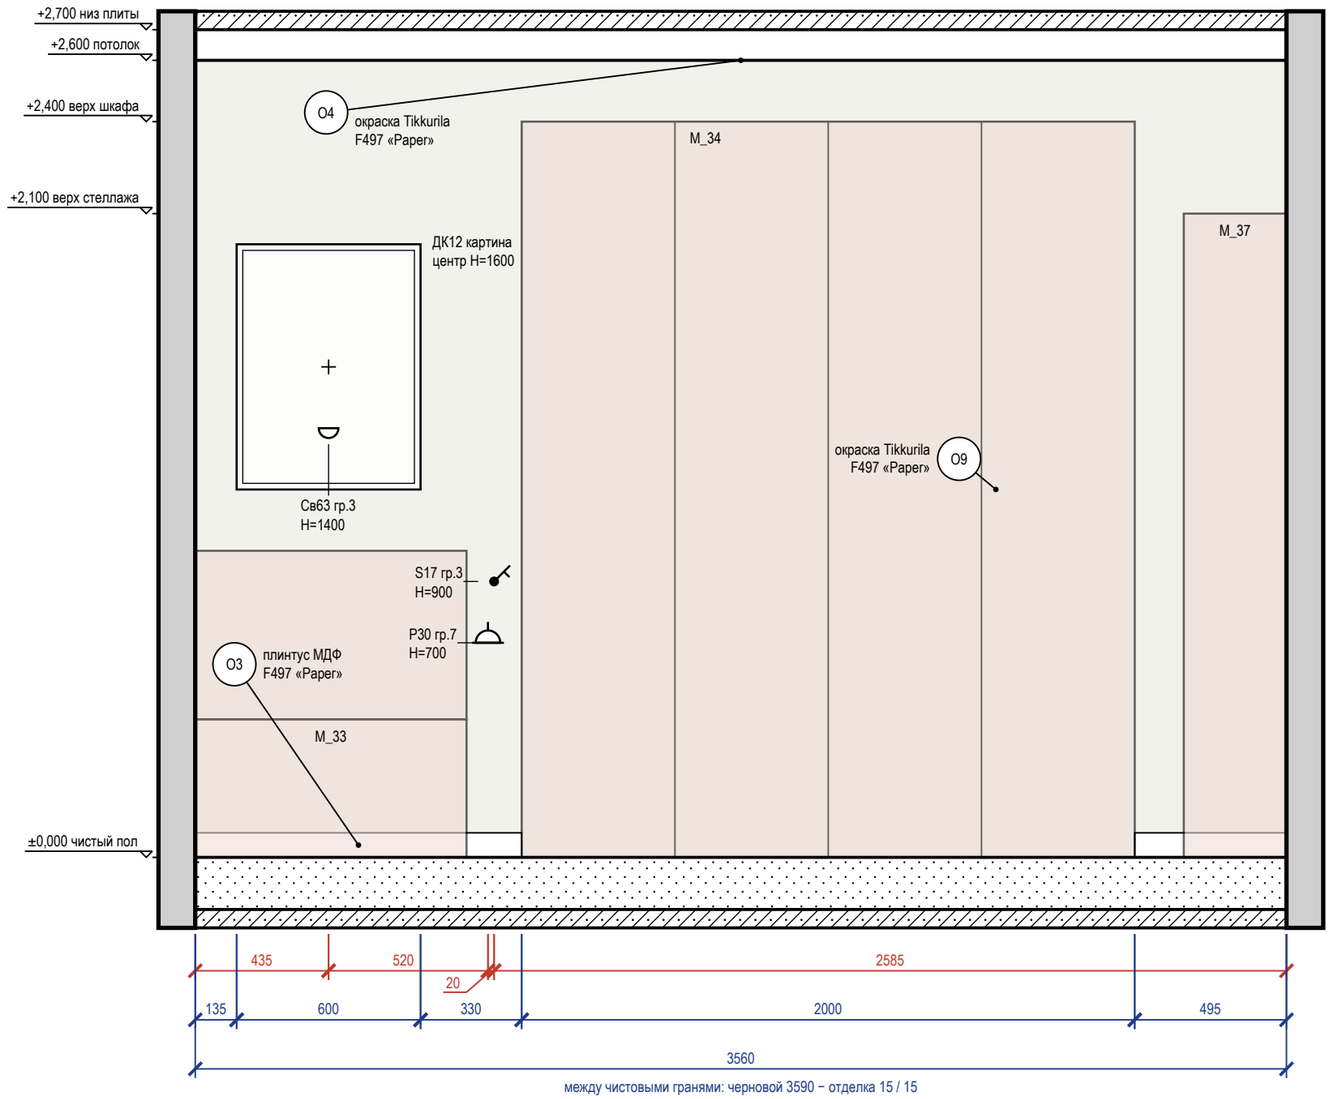


### Схема развёрток (М 1:100)

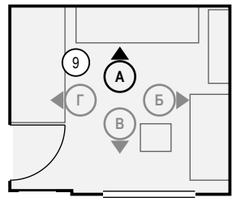


### Ведомость отделки (на листе)

| Марка | Поверхность | Материал, изделие | Цвет, код | Кол. |
|---|---|---|---|---|
| О3 | плинтус | плинтус МДФ, h 80 мм, аналог: плинтус МДФ под окраску 80×16 мм, полуглянцевая | Tikkurila F497 «Paper» | 1,6 м |
| О4 | потолок | окраска, Tikkurila Anti-Reflex 2, глубокоматовая, подготовка Q3 | Tikkurila F497 «Paper» | 11 м² |
| О9 | стены | окраска, Tikkurila Joker, шелковисто-матовая, подготовка К3 | Tikkurila F497 «Paper» | 9,3 м² |


### Примечания

1. Размеры — в мм от чистовых поверхностей стен; условные обозначения и общие указания — лист 3.
2. Картины и зеркала крепить к основанию по паспорту изделия (закладные и анкеры — в перечне скрытых работ); крест — ось центра предмета.


| | | | | | |
|---|---|---|---|---|---|
| | | | | | Проект: Четырёхкомнатная квартира — М 1:20 |
| | Лист | № док. | Подпись | Дата | |
| Дизайнер | Кырлан А.С. | | | 04.11.26 | Развёртка стены А. Детская 2 (пом. 9) |

| Стадия | Лист | Листов |
|---|---|---|
| П | 78 | 120 |

## Развёртка стены Б

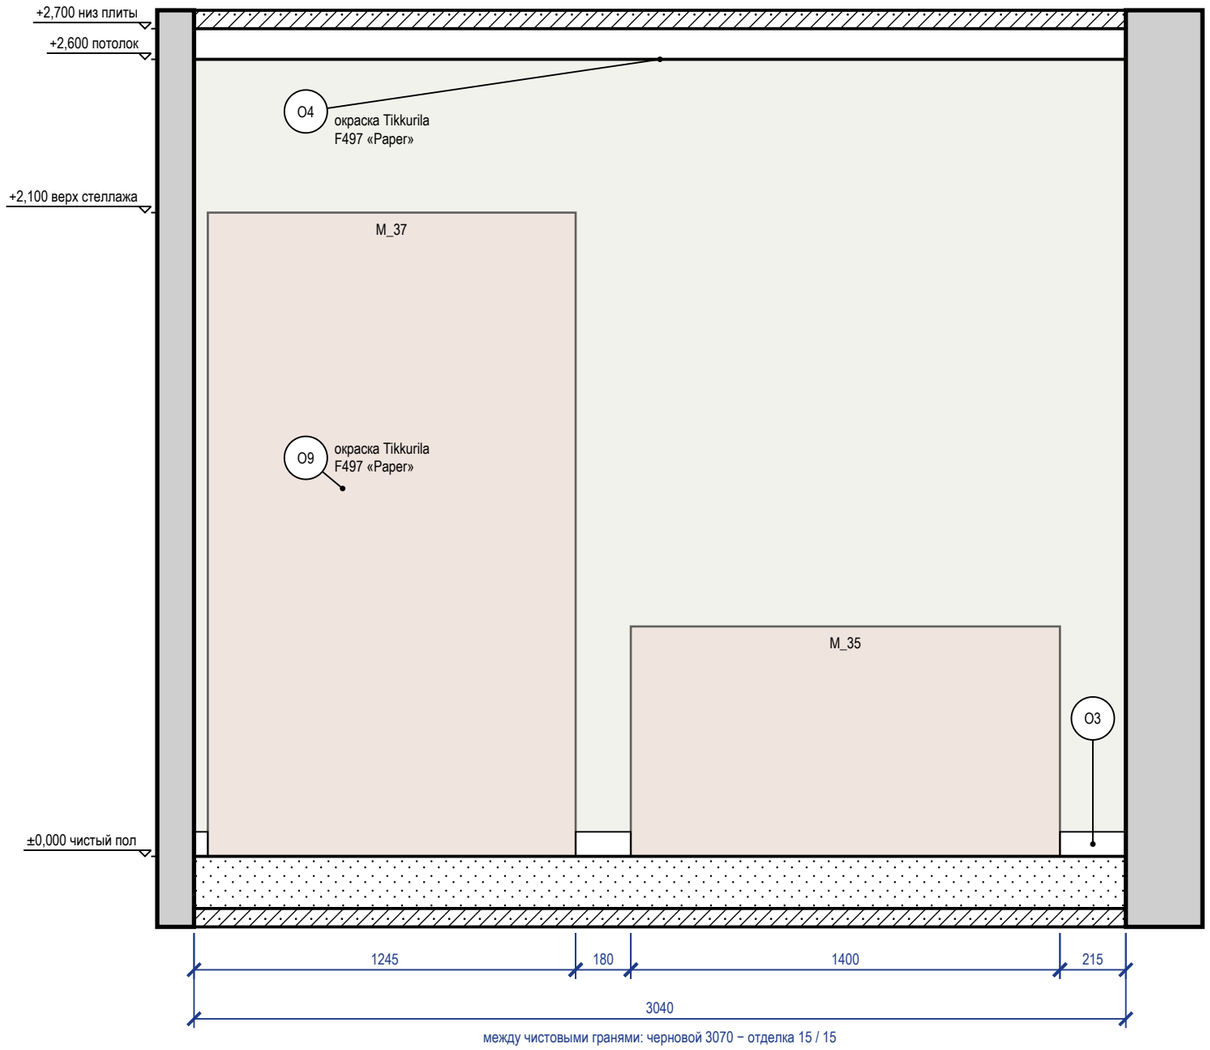


### Схема развёрток (М 1:100)

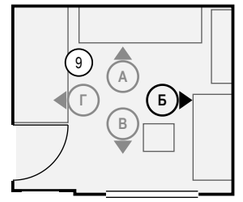


### Ведомость отделки (на листе)


| Марка | Поверхность | Материал, изделие | Цвет, код | Кол. |
|---|---|---|---|---|
| O3 | плинтус | плинтус МДФ, h 80 мм, аналог: плинтус МДФ под окраску 80×16 мм, полуглянцевая | Tikkurila F497 «Paper» | 0,4 м |
| O4 | потолок | окраска, Tikkurila Anti-Reflex 2, глубокоматовая, подготовка Q3 | Tikkurila F497 «Paper» | 11 м² |
| O9 | стены | окраска, Tikkurila Joker, шелковисто-матовая, подготовка К3 | Tikkurila F497 «Paper» | 7,9 м² |

### Примечания

1. Размеры — в мм от чистовых поверхностей стен; условные обозначения и общие указания — лист 3.
2. Стена Б показана двумя видами: здесь — архитектурная развёртка (мебель, отделка, проёмы, высоты), электроточки и выводы ВК с привязками и таблицей — на листе 80 («Привязки»).

| | | | | | | |
|---|---|---|---|---|---|---|
| | | | | | Проект: Четырёхкомнатная квартира | М 1:20 |
| | Лист | № док. | Подпись | Дата | | |
| Дизайнер | Кырлан А.С. | | | 04.11.26 | Развёртка стены Б. Детская 2 (пом. 9) | Стадия: П; Лист: 79; Листов: 120 |

## Развёртка стены Б: электроточки и выводы

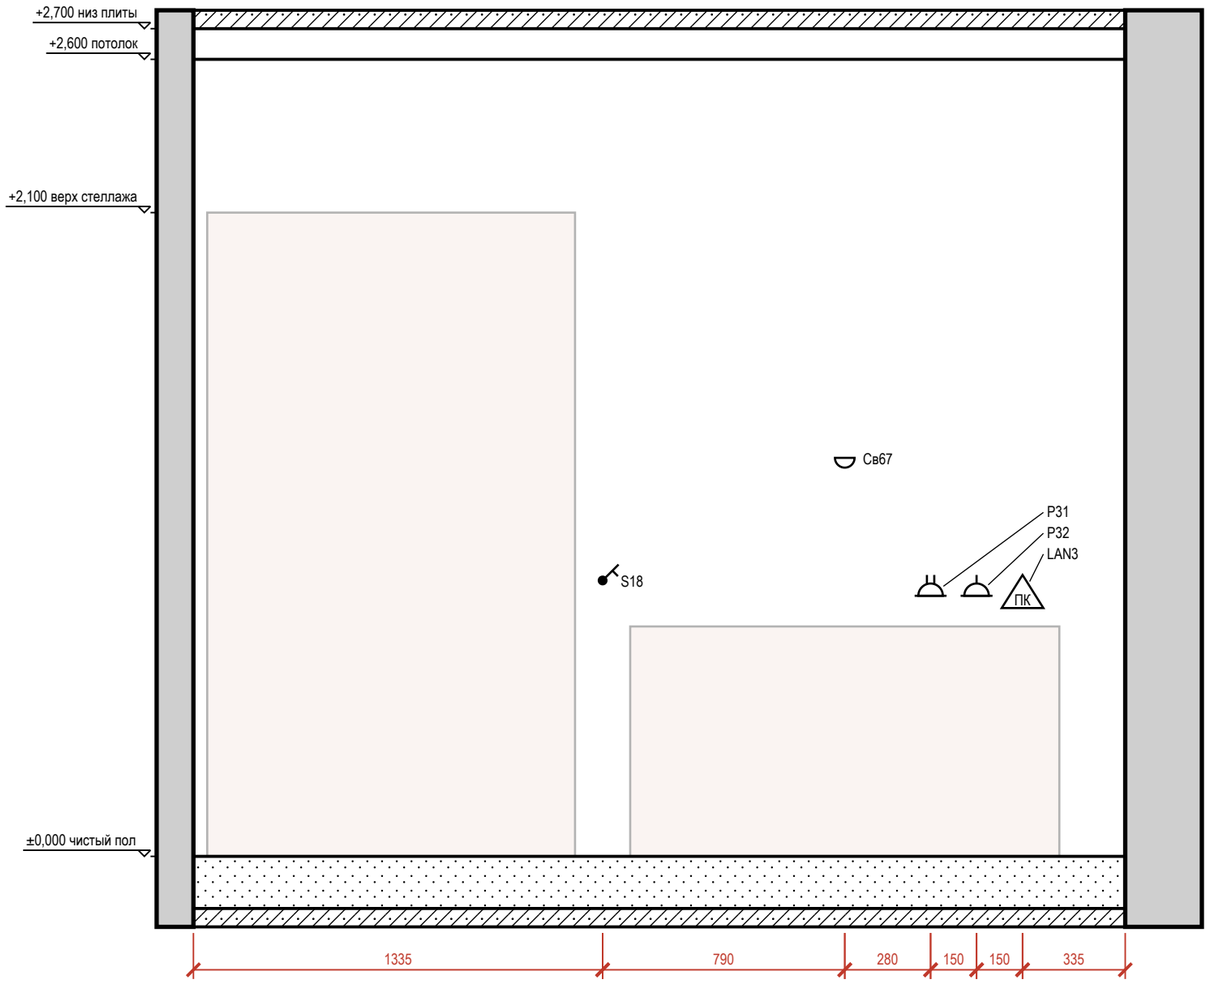


## Таблица привязок электроточек и выводов

| Марка | Назначение | От угла, мм | Н от пола, мм | Примечание |
|---|---|---|---|---|
| S18 | выключатель | 1335 | 900 | гр. 3 |
| Св67 | светильник настенный | 2125 | 1300 | гр. 3 |
| P31 | розетка: рабочий стол М_35 | 2405 | 850 | рамка 2 поста, гр. 7 |
| P32 | розетка: рабочий стол М_35 | 2555 | 850 | гр. 7 |
| LAN3 | розетка RJ45: рабочий стол М_35 | 2705 | 850 | |

## Условные обозначения

- розетка с заземляющим контактом; у знака — марка, ×N постов в рамке, гр. — группа щита, Н — высота оси, мм
- выключатель одноклавишный
- светильник настенный (бра), Н — высота оси
- ПК — розетка компьютерная RJ45
- привязки точек и выводов от угла и от пола, мм
- A — марка развёртки: буква стены, стрелка — взгляд

## Схема развёрток (М 1:50)





## Примечания


1. Вид «Привязки» стены Б — электроточки и выводы ВК; архитектурная развёртка (мебель, отделка, проёмы, высоты) — на листе 79. Мебель и приборы — подложкой для ориентира; их марки и обозначения мебели, проёмов и стен — там же.
2. Привязки — в мм: по горизонтали от левого чистового угла стены до оси изделия, Н — от чистого пола до оси; все точки — в таблице привязок. Красная цепочка — привязки по осям; точки ближе 120 мм одна к другой в цепочку не дробятся — их привязки только в таблице.
3. У знака — марка электроточки (Р — розетка, S — выключатель, Св — светильник, ЭВ — вывод кабеля); условные обозначения и общие указания — лист 3.

| | | | | | | |
|---|---|---|---|---|---|---|
| | | | | | Проект: Четырёхкомнатная квартира | М 1:20 |
| | Лист | № док. | Подпись | Дата | | |
| Дизайнер | Кырлан А.С. | | | 04.11.26 | Привязки электроточек, стена Б. Детская 2 (пом. 9) | Стадия: П; Лист: 80; Листов: 120 |

## Развёртка стены В

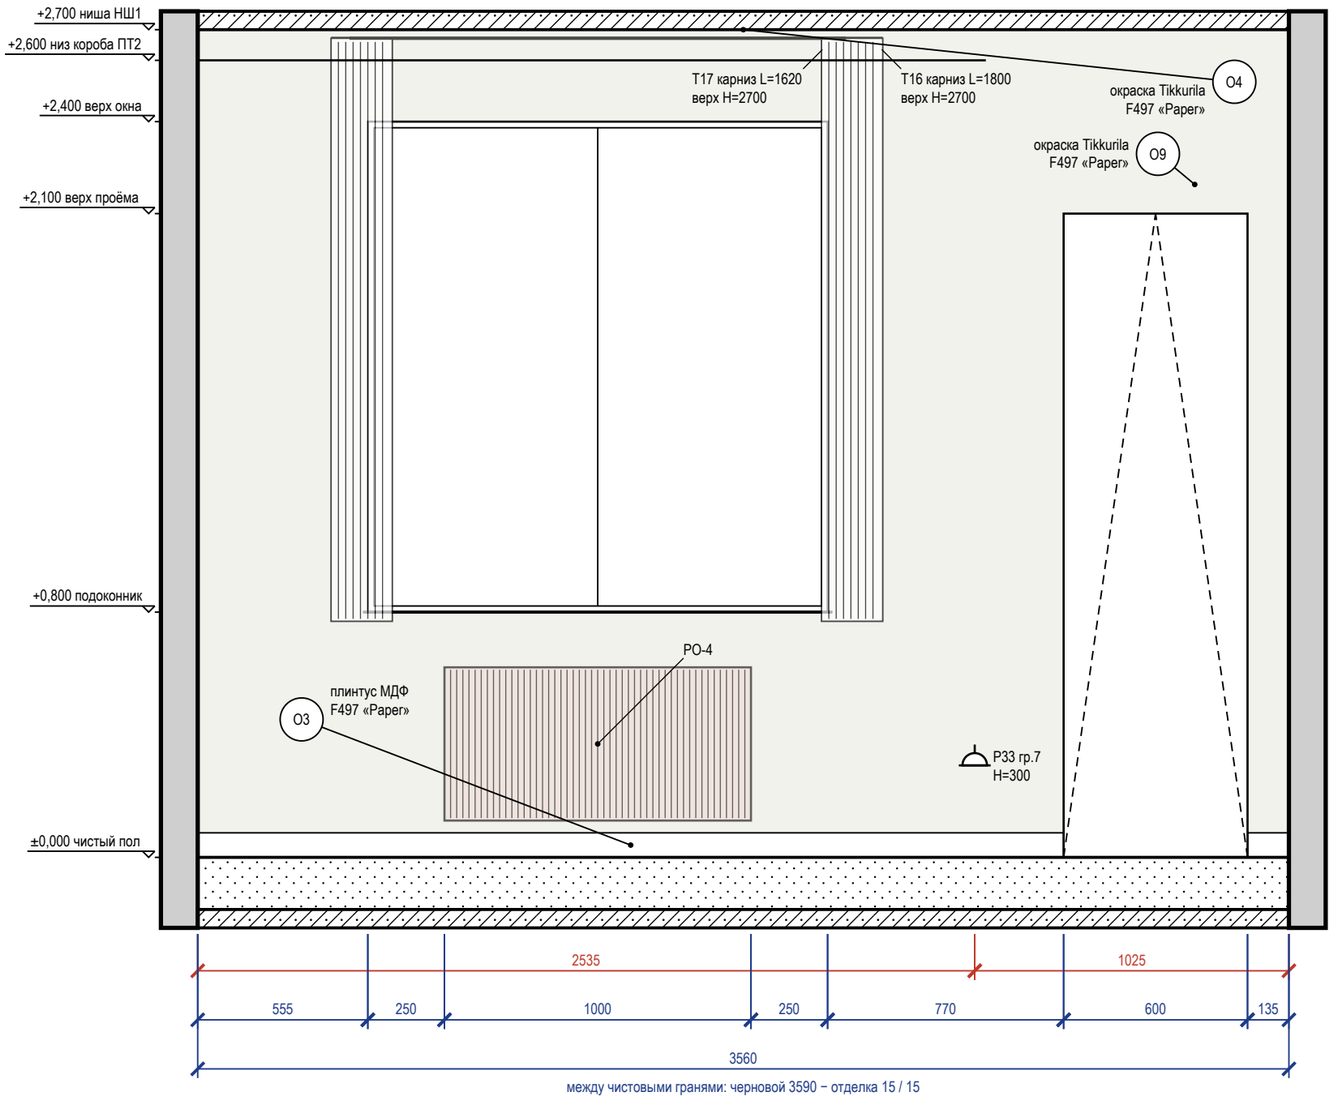


### Схема развёрток (М 1:100)

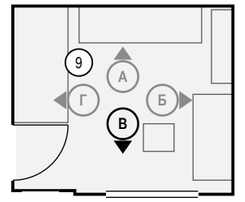


### Ведомость отделки (на листе)

| Марка | Поверхность | Материал, изделие | Цвет, код | Кол. |
|---|---|---|---|---|
| О3 | плинтус | плинтус МДФ, h 80 мм, аналог: плинтус МДФ под окраску 80×16 мм, полуглянцевая | Tikkurila F497 «Paper» | 3 м |
| О4 | потолок | окраска, Tikkurila Anti-Reflex 2, глубокоматовая, подготовка Q3 | Tikkurila F497 «Paper» | 11 м² |
| О9 | стены | окраска, Tikkurila Joker, шелковисто-матовая, подготовка К3 | Tikkurila F497 «Paper» | 6 м² |


### Примечания

1. Размеры — в мм от чистовых поверхностей стен; условные обозначения и общие указания — лист 3.
2. Карнизы (шины) — по ведомости текстиля декоратора: длина L и верх H на развёртке — те же числа, что в ведомости; крепление — до окраски потолка.


| | | | | | | |
|---|---|---|---|---|---|---|
| | | | | | Проект: Четырёхкомнатная квартира | М 1:20 |
| | Лист | № док. | Подпись | Дата | | |
| Дизайнер | Кырлан А.С. | | | 04.11.26 | Развёртка стены В. Детская 2 (пом. 9) | |

| Стадия | Лист | Листов |
|---|---|---|
| П | 81 | 120 |

## Развёртка стены Г

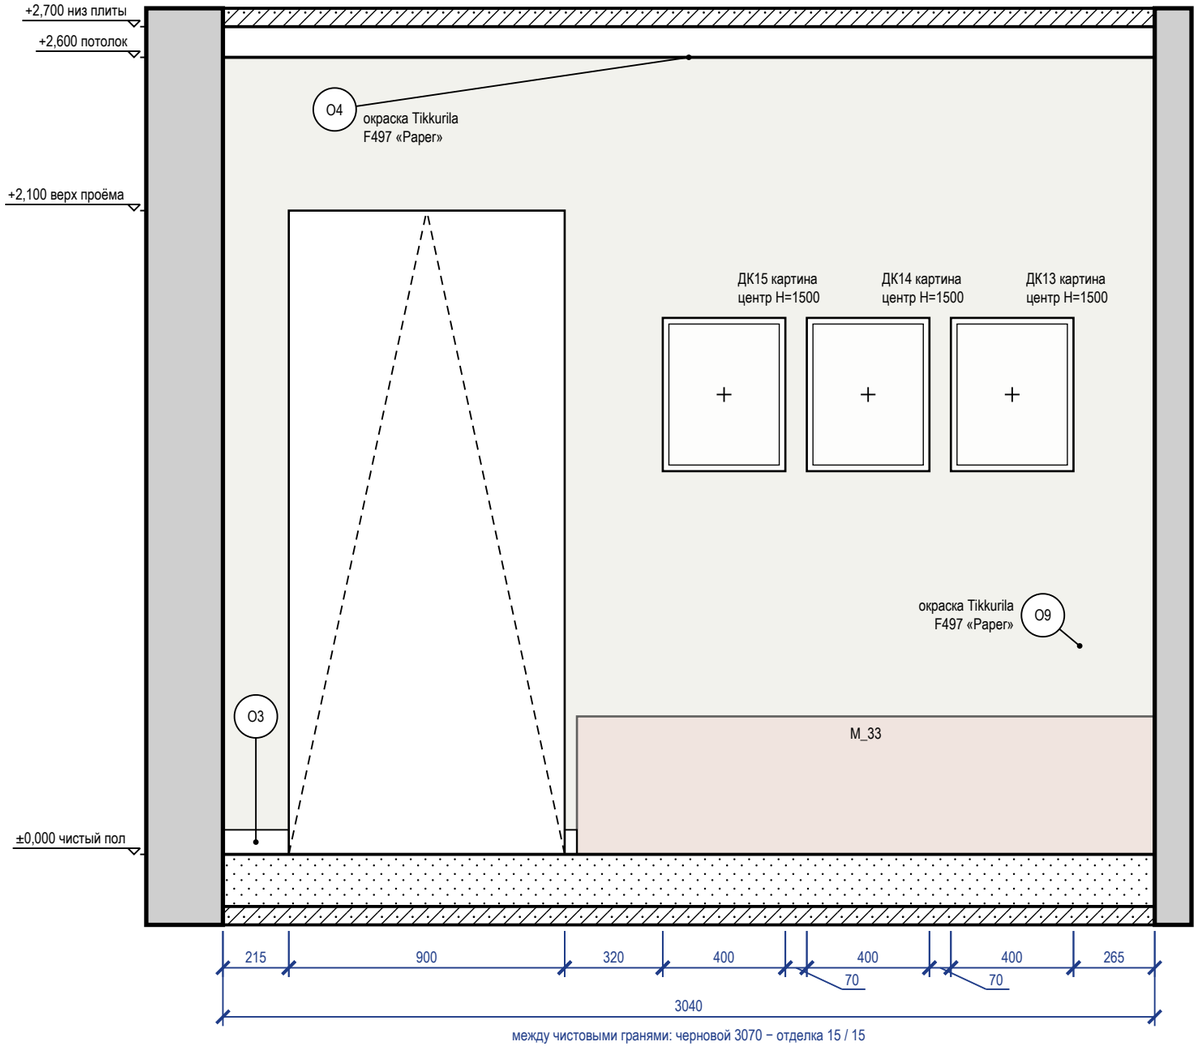


### Схема развёрток (М 1:100)

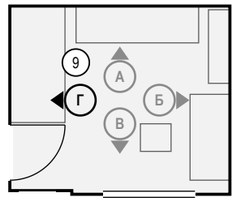


### Ведомость отделки (на листе)

| Марка | Поверхность | Материал, изделие | Цвет, код | Кол. |
|---|---|---|---|---|
| О3 | плинтус | плинтус МДФ, h 80 мм, аналог: плинтус МДФ под окраску 80×16 мм, полуглянцевая | Tikkurila F497 «Paper» | 0,3 м |
| О4 | потолок | окраска, Tikkurila Anti-Reflex 2, глубокоматовая, подготовка Q3 | Tikkurila F497 «Paper» | 11 м² |
| О9 | стены | окраска, Tikkurila Joker, шелковисто-матовая, подготовка К3 | Tikkurila F497 «Paper» | 6 м² |


### Примечания

1. Размеры — в мм от чистовых поверхностей стен; условные обозначения и общие указания — лист 3.
2. Картины и зеркала крепить к основанию по паспорту изделия (закладные и анкеры — в перечне скрытых работ); крест — ось центра предмета.

| | | | | | |
|---|---|---|---|---|---|
| | | | | | Проект: Четырёхкомнатная квартира — М 1:20 |
| | Лист | № док. | Подпись | Дата | Развёртка стены Г. Детская 2 (пом. 9) |
| Дизайнер | Кырлан А.С. | | | 04.11.26 | |


| Стадия | Лист | Листов |
|---|---|---|
| П | 82 | 120 |

## Развёртка стены А

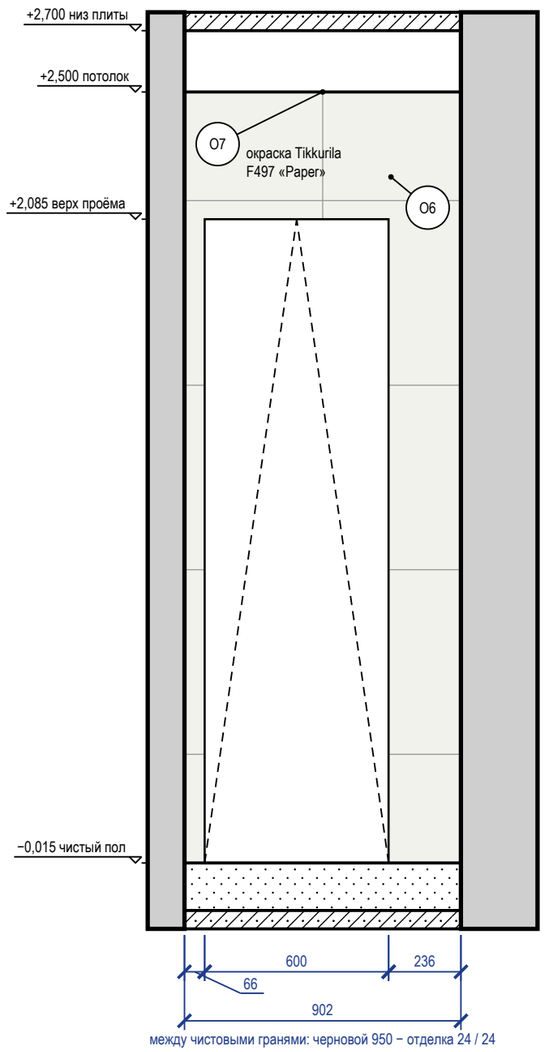



между чистовыми гранями: черновой 950 − отделка 24 / 24

## Развёртка стены Б

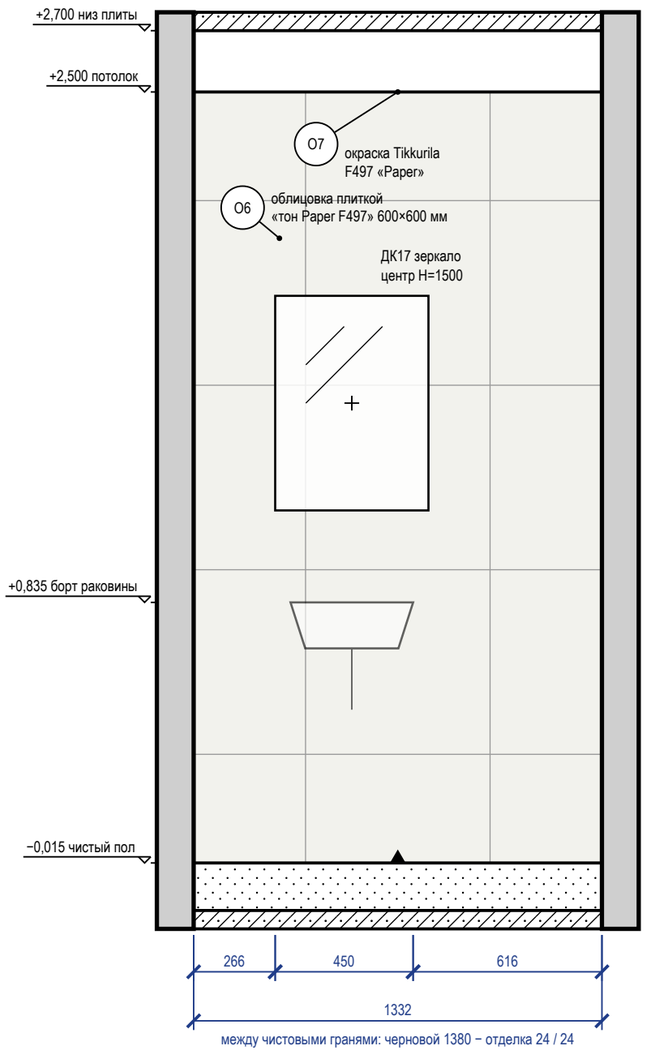



между чистовыми гранями: черновой 1380 − отделка 24 / 24

## Развёртка стены В

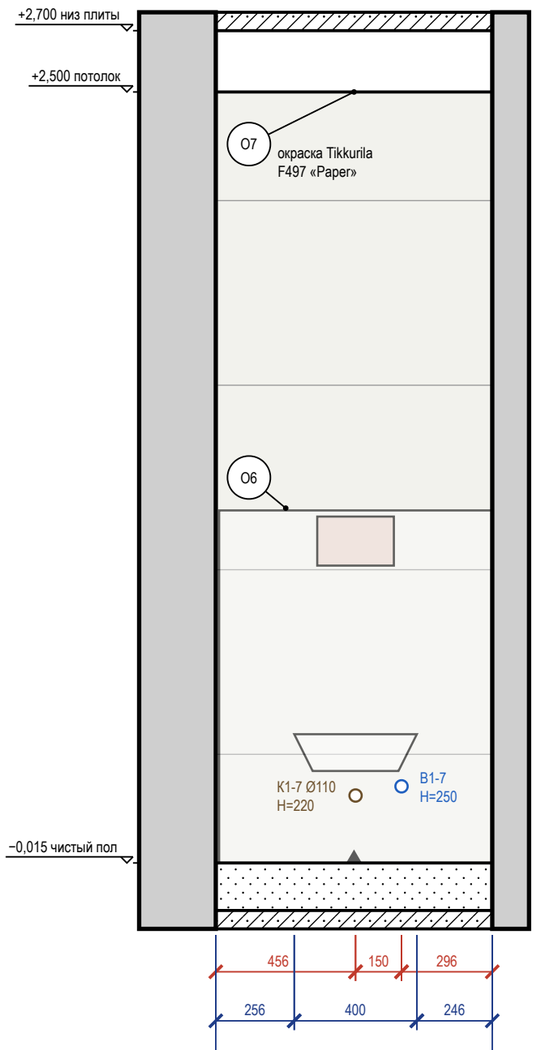


между чистовыми гранями: черновой 950 − отделка 24 / 24

### Схема развёрток (М 1:100)

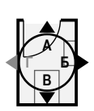


### Ведомость отделки (на листе)


| Марка | Поверхность | Материал, изделие | Цвет, код | Кол. |
|---|---|---|---|---|
| О6 | стены | облицовка плиткой, 600×600×9 мм, аналог: керамогранит матовый, тон F497, затирка CG2WA | #F1F1EC «тон Paper F497» | 6,6 м² |
| О7 | потолок | окраска, Tikkurila Luja 7, матовая, подготовка Q3 | Tikkurila F497 «Paper» | 1,3 м² |

### Примечания

1. Размеры — в мм от чистовых поверхностей стен; условные обозначения и общие указания — лист 3.
2. Стена Б показана двумя видами: здесь — архитектурная развёртка (мебель, отделка, проёмы, высоты), электроточки и выводы ВК с привязками и таблицей — на листе 84 («Привязки»).
3. Облицовка — по сетке швов 2 мм, раскладка от оси стены (треугольник у пола), по высоте — от середины облицовки, подрезки у пола и у потолка поровну; подрезки — по листу раскладки плитки.
4. Гидроизоляция в 2 слоя, заход на стены 200 мм — до облицовки, с актом скрытых работ и тестом проливом (узел — на листе узлов).
5. Картины и зеркала крепить к основанию по паспорту изделия (закладные и анкеры — в перечне скрытых работ); крест — ось центра предмета.

| | | | | | |
|---|---|---|---|---|---|
| | | | | | Проект: Четырёхкомнатная квартира — М 1:20 |
| | Лист | № док. | Подпись | Дата | |
| Дизайнер | Кырлан А.С. | | | 04.11.26 | Развёртки стен А, Б, В. Санузел (пом. 10) |
| | | | | | Стадия: П; Лист: 83; Листов: 120 |

## Развёртка стены Б: электроточки и выводы

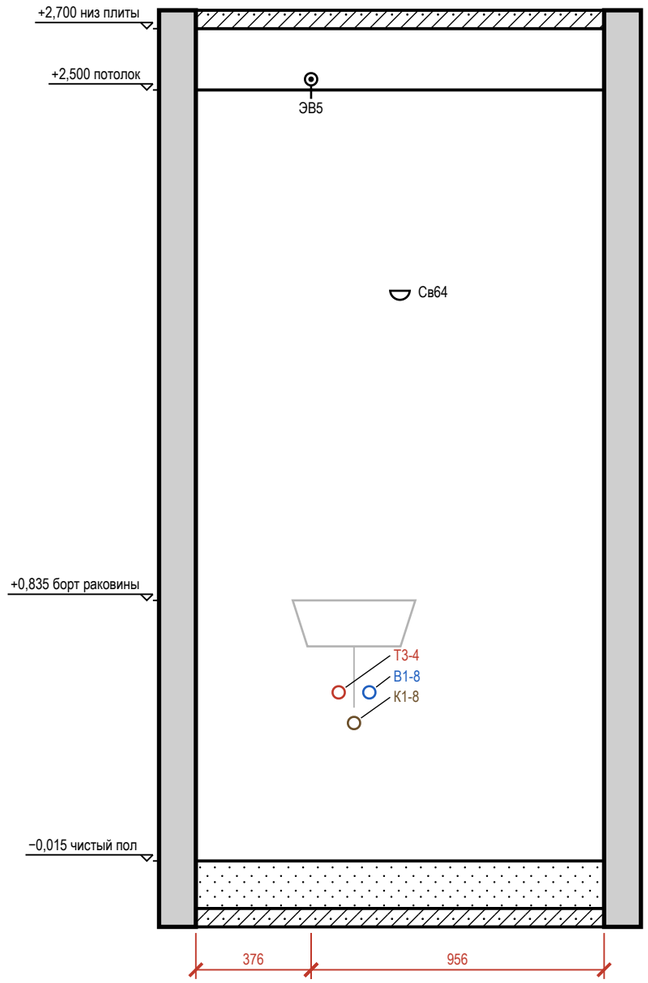



## Таблица привязок электроточек и выводов

| Марка | Назначение | От угла, мм | Н от пола, мм | Примечание |
|---|---|---|---|---|
| ЭВ5 | вывод кабеля: вентилятор ВР3 (таймер выбега) | 376 | 2550 | гр. 4 |
| Т3-4 | горячая вода — умывальник | 466 | 550 | межос. 100 |
| К1-8 | канализация — умывальник | 516 | 450 | Ø40 |
| В1-8 | холодная вода — умывальник | 566 | 550 | межос. 100 |
| Св64 | светильник настенный | 666 | 1860 | гр. 4 |

## Условные обозначения

- вывод кабеля для подключения прибора (без розетки), марка ЭВ
- светильник настенный (бра), Н — высота оси
- вывод В1 (код — в ведомости привязок)
- вывод Т3 (код — в ведомости привязок)
- вывод К1 (код — в ведомости привязок)
- привязки точек и выводов от угла и от пола, мм
- А — марка развёртки: буква стены, стрелка — взгляд

## Схема развёрток (М 1:50)

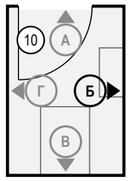



## Примечания

1. Вид «Привязки» стены Б — электроточки и выводы ВК; архитектурная развёртка (мебель, отделка, проёмы, высоты) — на листе 83. Мебель и приборы — подложкой для ориентира; их марки и обозначения мебели, проёмов и стен — там же.
2. Привязки — в мм: по горизонтали от левого чистового угла стены до оси изделия, Н — от чистого пола до оси; все точки — в таблице привязок. Красная цепочка — привязки по осям; точки ближе 120 мм одна к другой в цепочку не дробятся — их привязки только в таблице.
3. У знака — марка электроточки (Р — розетка, S — выключатель, Св — светильник, ЭВ — вывод кабеля); условные обозначения и общие указания — лист 3.
4. Коды выводов ВК: В1 — холодная вода, Т3 — горячая вода, К1 — канализация; номер после дефиса — номер вывода на листе выводов сантехники.

| | | | | | |
|---|---|---|---|---|---|
| | | | | | Проект: Четырёхкомнатная квартира — М 1:20 |
| | Лист | № док. | Подпись | Дата | |
| Дизайнер | Кырлан А.С. | | | 04.11.26 | Привязки электроточек и выводов ВК, стена Б. Санузел (пом. 10) |

| Стадия | Лист | Листов |
|---|---|---|
| П | 84 | 120 |

## Развёртка стены Г

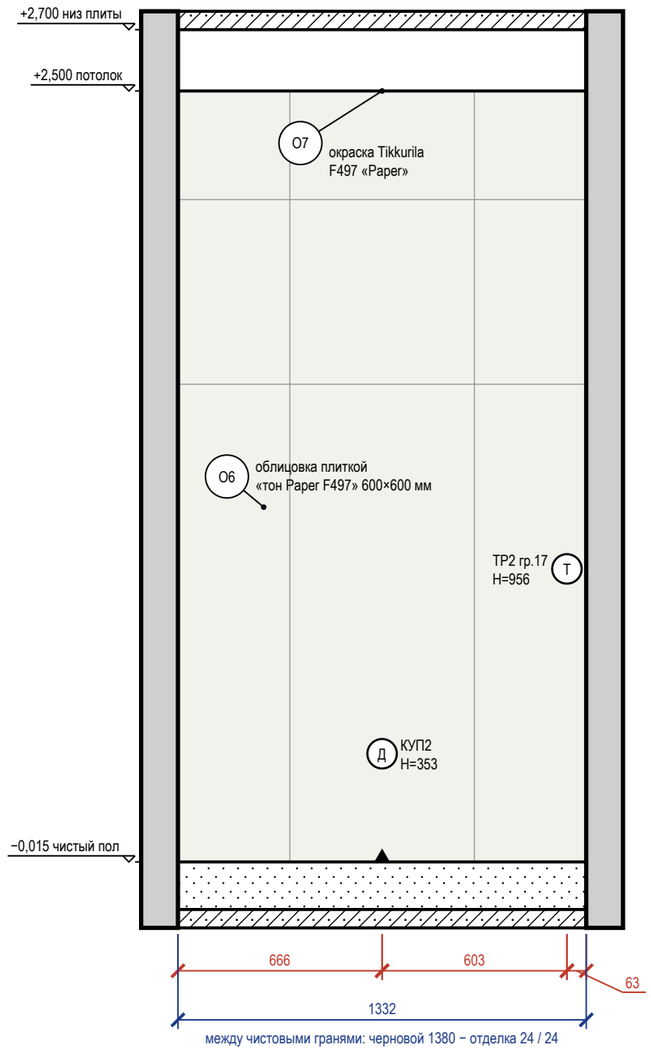


### Схема развёрток (М 1:100)




### Ведомость отделки (на листе)


| Марка | Поверхность | Материал, изделие | Цвет, код | Кол. |
|---|---|---|---|---|
| О6 | стены | облицовка плиткой, 600×600×9 мм, аналог: керамогранит матовый, тон F497, затирка CG2WA | #F1F1EC «тон Paper F497» | 3,3 м² |
| О7 | потолок | окраска, Tikkurila Luja 7, матовая, подготовка Q3 | Tikkurila F497 «Paper» | 1,3 м² |

### Примечания


1. Размеры — в мм от чистовых поверхностей стен; условные обозначения и общие указания — лист 3.
2. Облицовка — по сетке швов 2 мм, раскладка от оси стены (треугольник у пола), по высоте — от середины облицовки, подрезки у пола и у потолка поровну; подрезки — по листу раскладки плитки.
3. Гидроизоляция в 2 слоя, заход на стены 200 мм — до облицовки, с актом скрытых работ и тестом проливом (узел — на листе узлов).

| | | | | | | |
|---|---|---|---|---|---|---|
| | | | | | Проект: Четырёхкомнатная квартира | М 1:20 |
| | Лист | № док. | Подпись | Дата | | |
| Дизайнер | Кырлан А.С. | | | 04.11.26 | Развёртка стены Г. Санузел (пом. 10) | Стадия: П; Лист: 85; Листов: 120 |

## Развёртка стены А

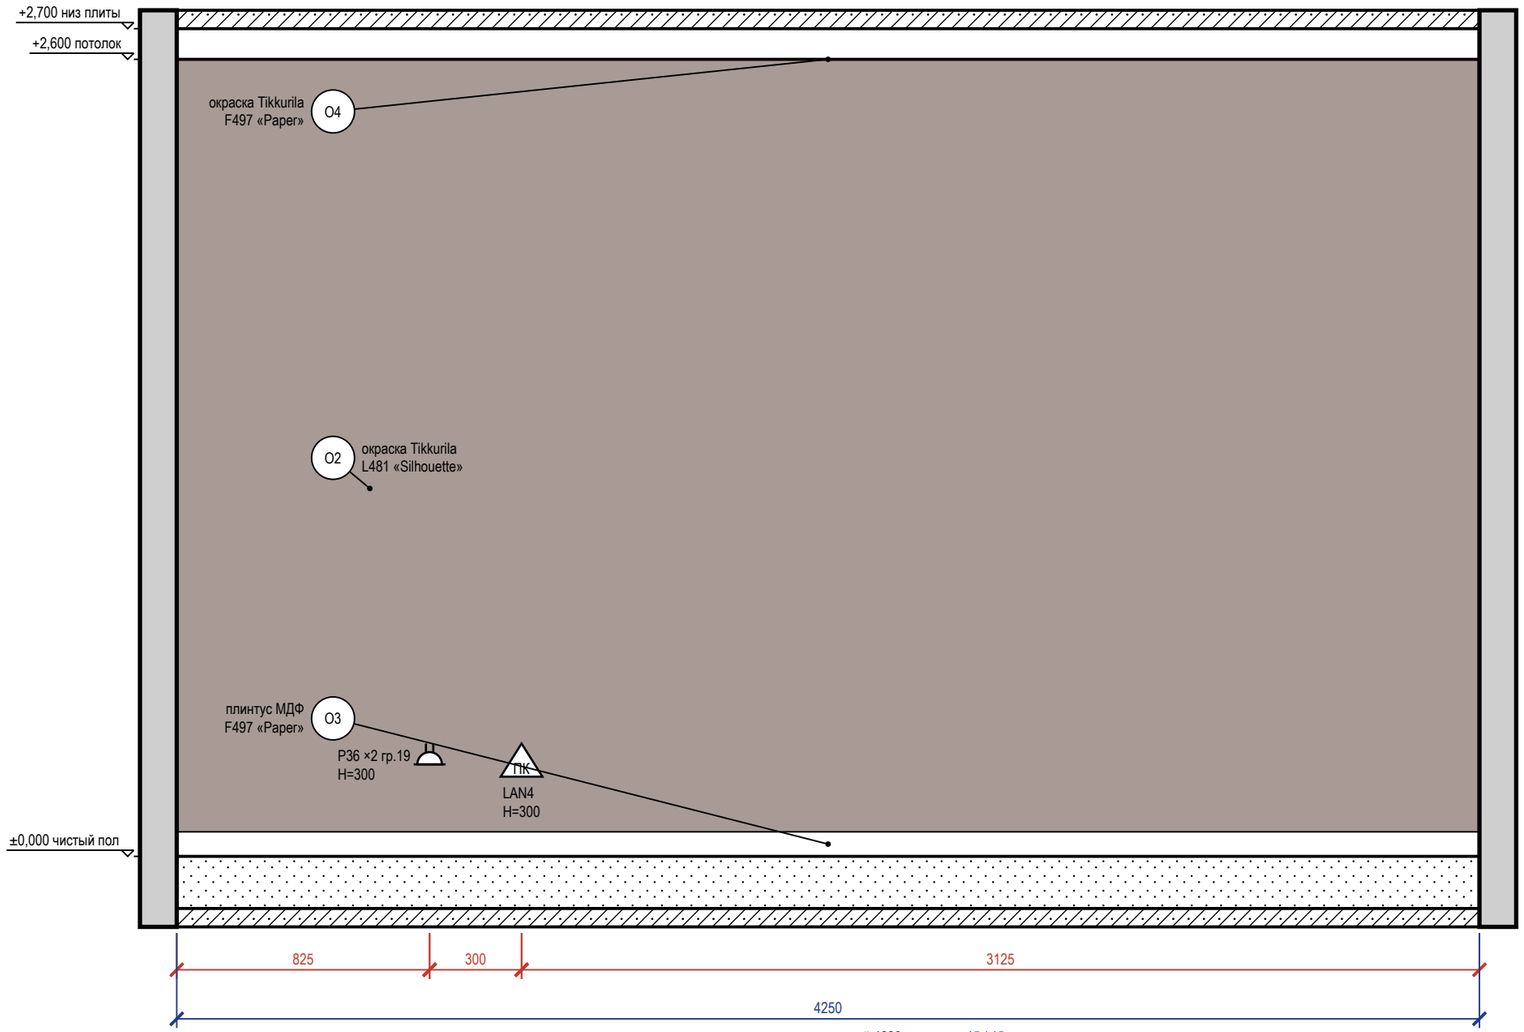


### Схема развёрток (М 1:100)

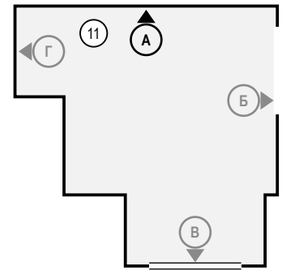


### Ведомость отделки (на листе)


| Марка | Поверхность | Материал, изделие | Цвет, код | Кол. |
|---|---|---|---|---|
| О2 | акцентная стена | окраска, Tikkurila Optiva 5 Matt, аналог: интерьерная краска, класс 2 по EN 13300, глубокоматовая/матовая, база С, матовая, подготовка К3 | Tikkurila L481 «Silhouette» | 11,1 м² |
| О3 | плинтус | плинтус МДФ, h 80 мм, аналог: плинтус МДФ под окраску 80×16 мм, полуглянцевая | Tikkurila F497 «Paper» | 4,3 м |
| О4 | потолок | окраска, Tikkurila Anti-Reflex 2, глубокоматовая, подготовка Q3 | Tikkurila F497 «Paper» | 14,6 м² |

### Примечания


1. Размеры — в мм от чистовых поверхностей стен; условные обозначения и общие указания — лист 3.

| | | | | | |
|---|---|---|---|---|---|
| | | | | | Проект: Четырёхкомнатная квартира — М 1:20 |
| | Лист | № док. | Подпись | Дата | |
| Дизайнер | Кырлан А.С. | | | 04.11.26 | Развёртка стены А. Гостиная (пом. 11) |
| | | | | | Стадия: П; Лист: 86; Листов: 120 |

## Развёртка стены Б

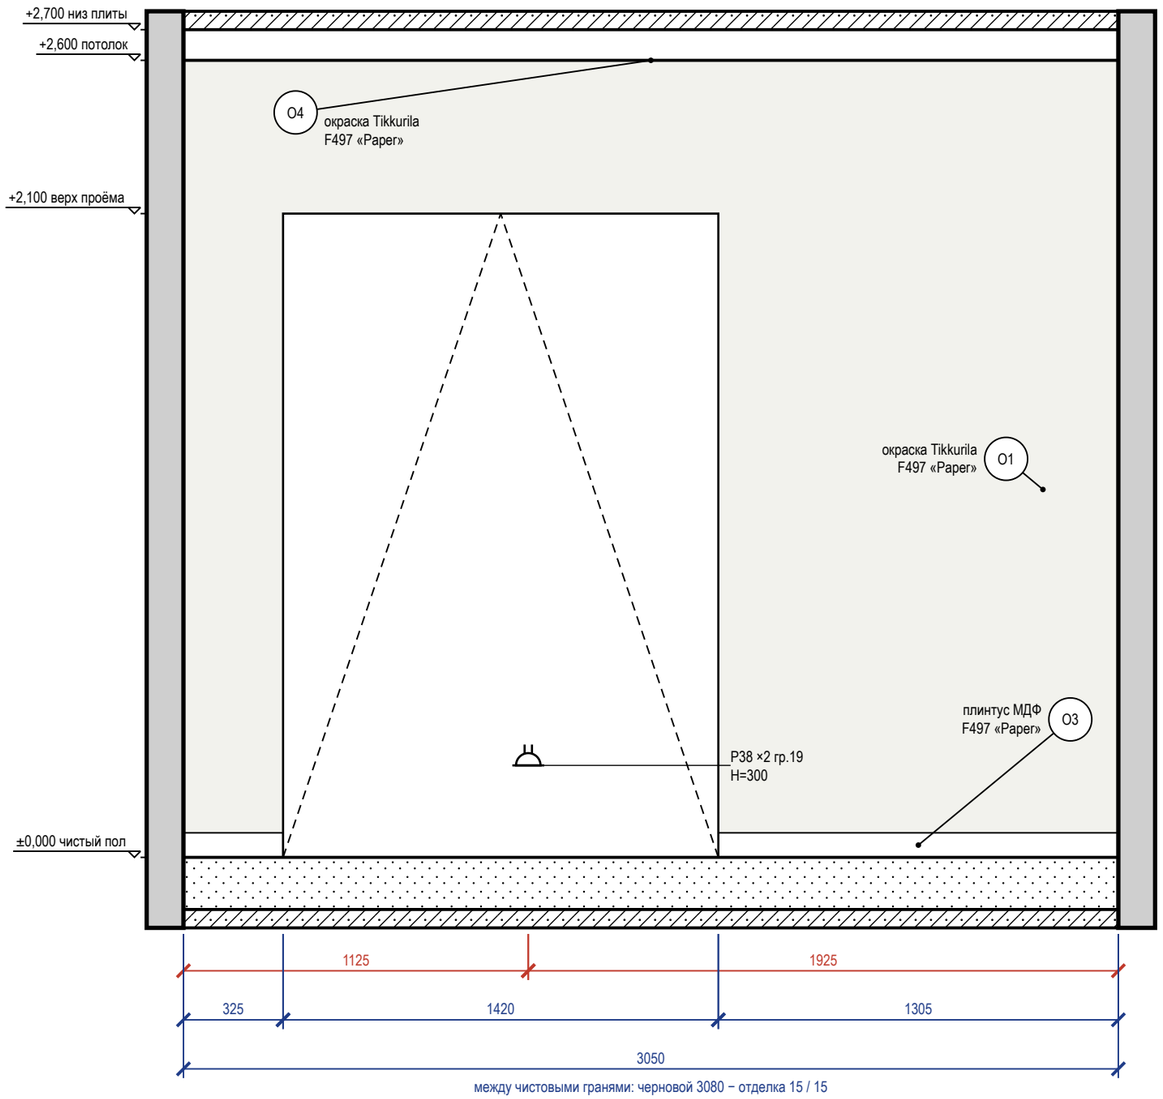


### Схема развёрток (М 1:100)

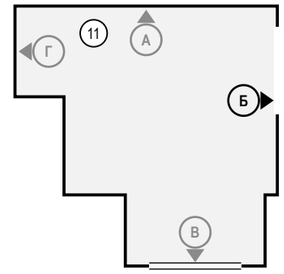


### Ведомость отделки (на листе)


| Марка | Поверхность | Материал, изделие | Цвет, код | Кол. |
|---|---|---|---|---|
| О1 | стены | окраска, Tikkurila Optiva 5 Matt, матовая, подготовка К3 | Tikkurila F497 «Paper» | 4,9 м² |
| О3 | плинтус | плинтус МДФ, h 80 мм, аналог: плинтус МДФ под окраску 80×16 мм, полуглянцевая | Tikkurila F497 «Paper» | 1,6 м |
| О4 | потолок | окраска, Tikkurila Anti-Reflex 2, глубокоматовая, подготовка Q3 | Tikkurila F497 «Paper» | 14,6 м² |

### Примечания


1. Размеры — в мм от чистовых поверхностей стен; условные обозначения и общие указания — лист 3.

| | | | | | | |
|---|---|---|---|---|---|---|
| | | | | | Проект: Четырёхкомнатная квартира | М 1:20 |
| | Лист | № док. | Подпись | Дата | | |
| Дизайнер | Кырлан А.С. | | | 04.11.26 | Развёртка стены Б. Гостиная (пом. 11) | |
| | | | | | Стадия: П; Лист: 87; Листов: 120 | |


## Развёртка стены В

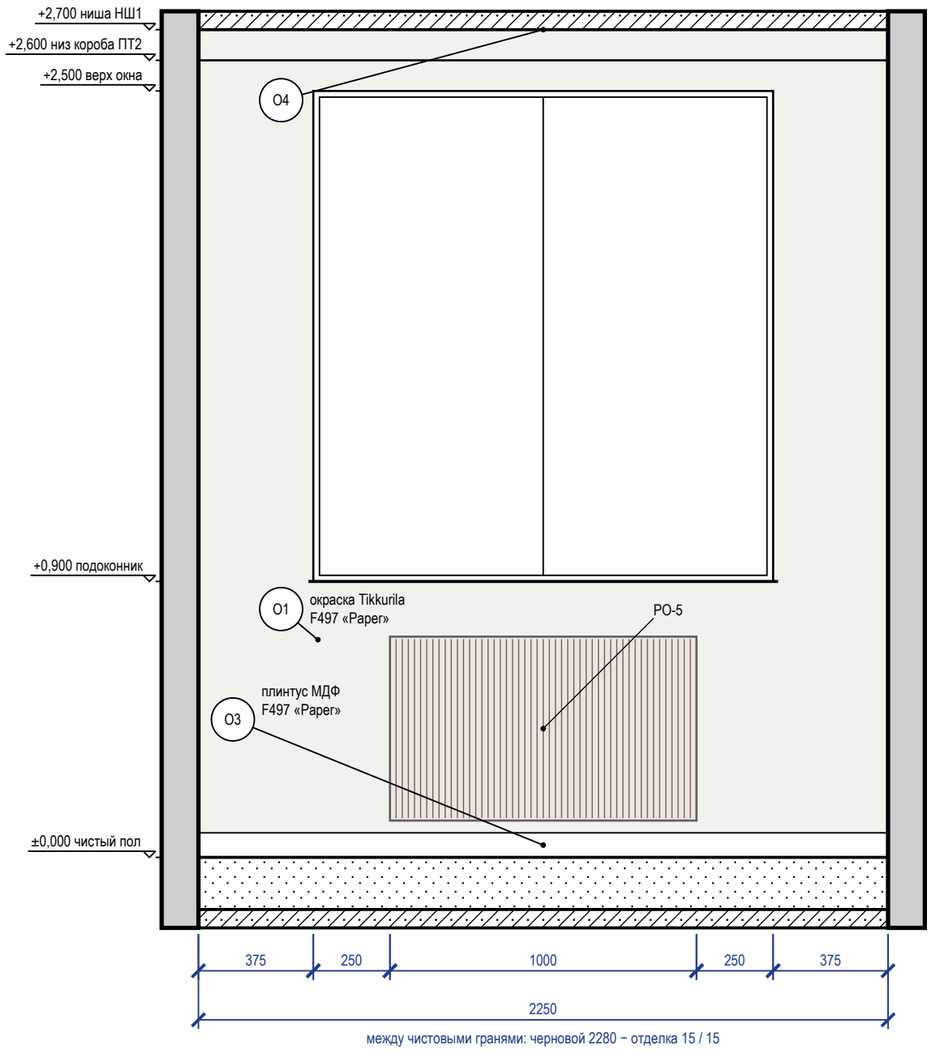


## Развёртка стены Г

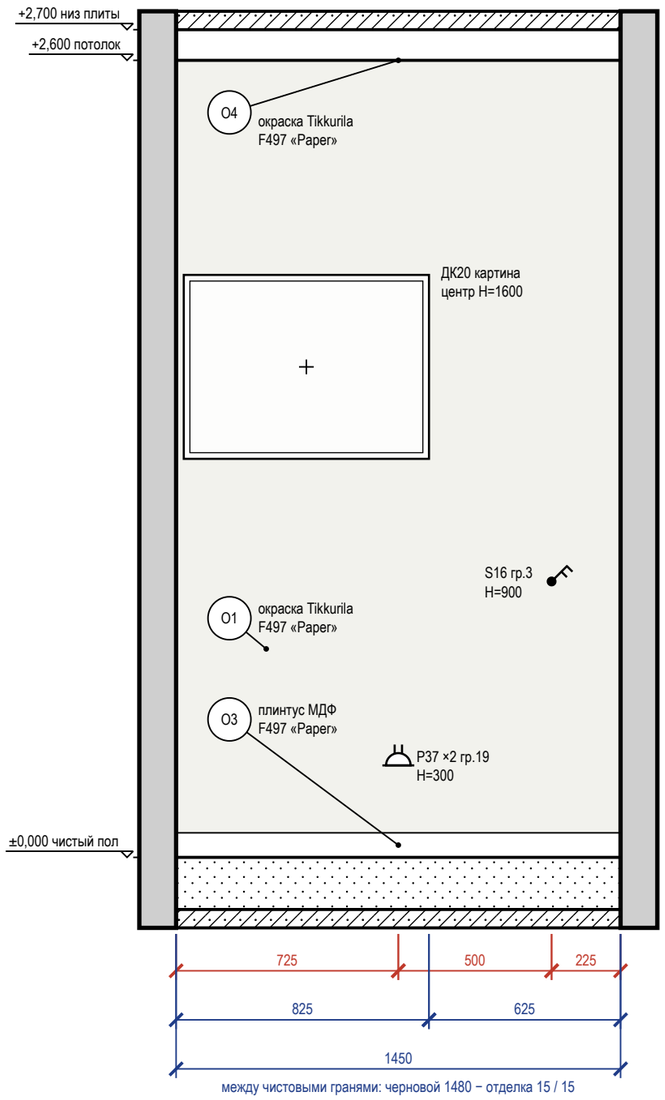


## Схема развёрток (М 1:100)

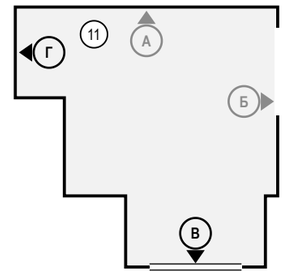


## Ведомость отделки (на листе)

| Марка | Поверхность | Материал, изделие | Цвет, код | Кол. |
|---|---|---|---|---|
| О1 | стены | окраска, Tikkurila Optiva 5 Matt, матовая, подготовка К3 | Tikkurila F497 «Paper» | 7,4 м² |
| О3 | плинтус | плинтус МДФ, h 80 мм, аналог: плинтус МДФ под окраску 80×16 мм, полуглянцевая | Tikkurila F497 «Paper» | 3,7 м |
| О4 | потолок | окраска, Tikkurila Anti-Reflex 2, глубокоматовая, подготовка Q3 | Tikkurila F497 «Paper» | 14,6 м² |

## Примечания

1. Размеры — в мм от чистовых поверхностей стен; условные обозначения и общие указания — лист 3.
2. Картины и зеркала крепить к основанию по паспорту изделия (закладные и анкеры — в перечне скрытых работ); крест — ось центра предмета.


| | | | | |
|---|---|---|---|---|
| | Лист | № док. | Подпись | Дата |
| Дизайнер | Кырлан А.С. | | | 04.11.26 |

Проект: Четырёхкомнатная квартира — **М 1:20**

Развёртки стен В, Г. Гостиная (пом. 11)


| Стадия | Лист | Листов |
|---|---|---|
| П | 88 | 120 |

## Развёртка стены А

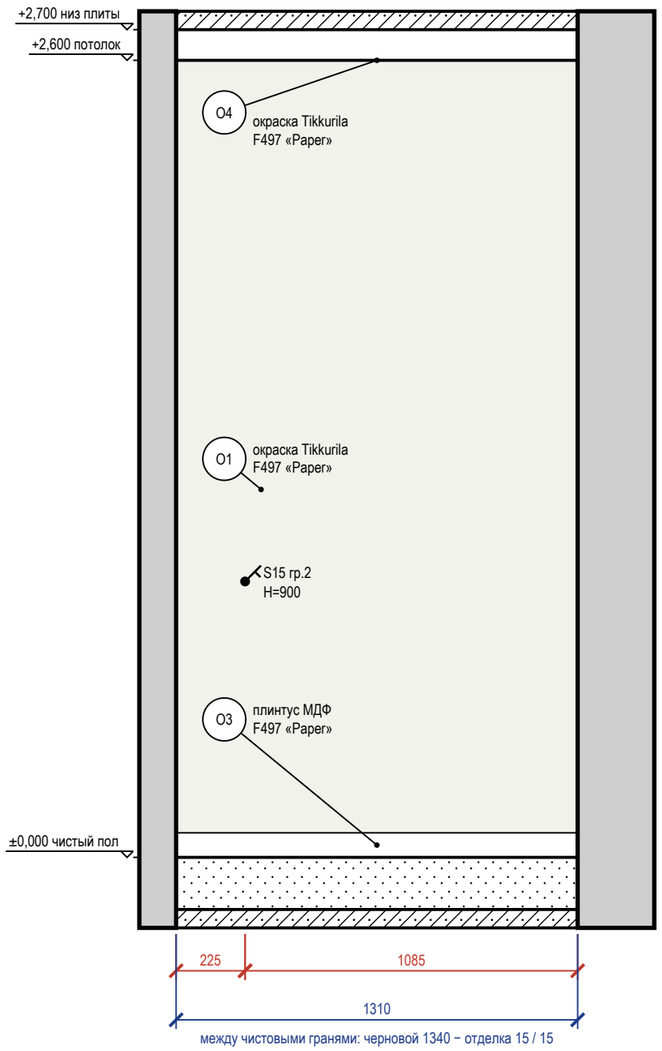



между чистовыми гранями: черновой 1340 − отделка 15 / 15

## Развёртка стены Б

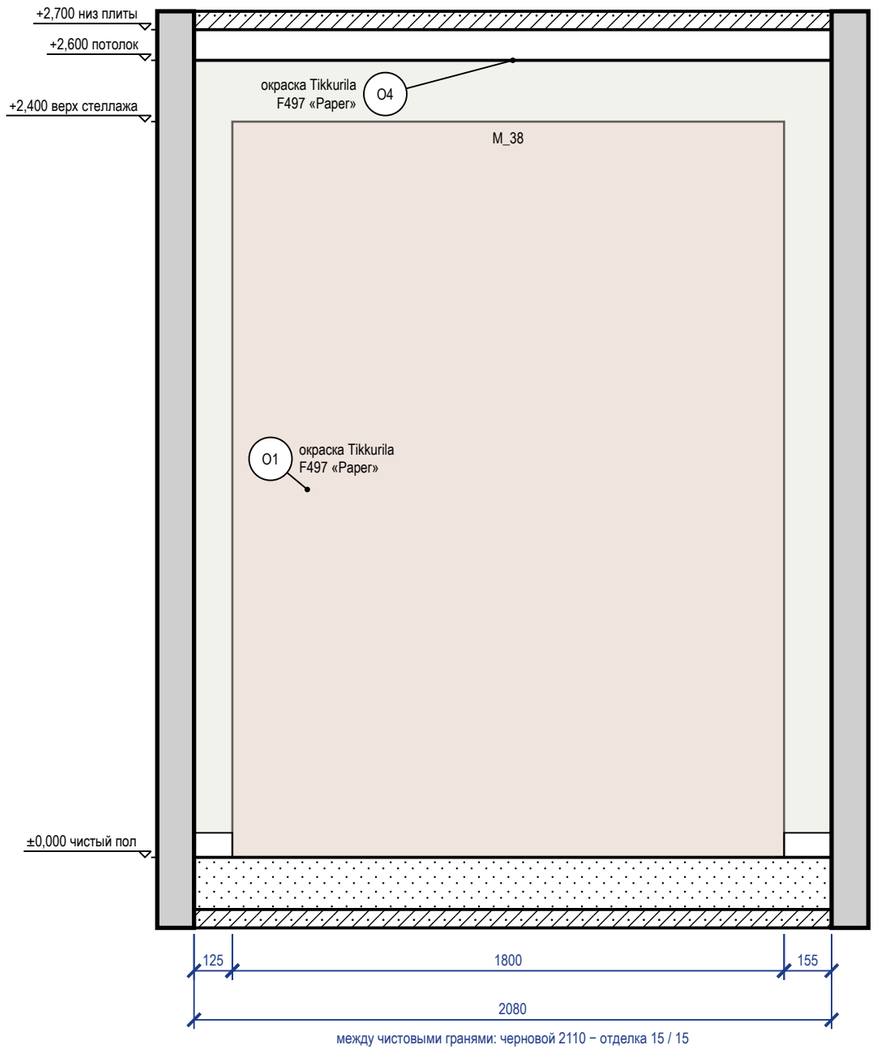



между чистовыми гранями: черновой 2110 − отделка 15 / 15

## Развёртка стены В

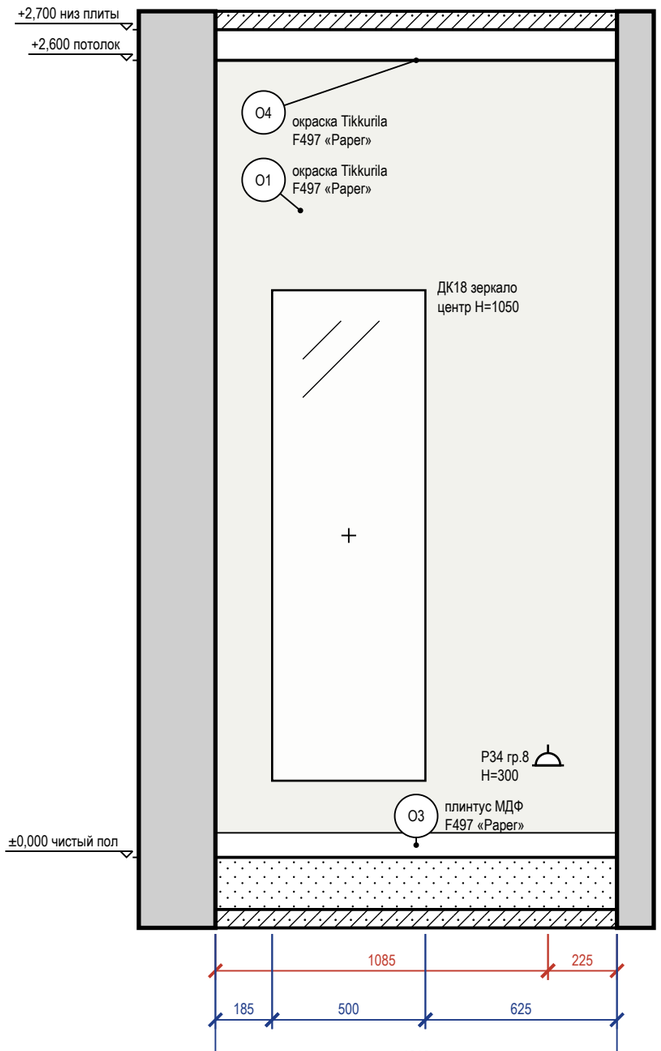


между чистовыми гранями: черновой 1340 − отделка 15 / 15

### Схема развёрток (М 1:100)

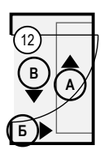


### Ведомость отделки (на листе)


| Марка | Поверхность | Материал, изделие | Цвет, код | Кол. |
|---|---|---|---|---|
| О1 | стены | окраска, Tikkurila Optiva 5 Matt, матовая, подготовка К3 | Tikkurila F497 «Paper» | 12,2 м² |
| О3 | плинтус | плинтус МДФ, h 80 мм, аналог: плинтус МДФ под окраску 80×16 мм, полуглянцевая | Tikkurila F497 «Paper» | 2,9 м |
| О4 | потолок | окраска, Tikkurila Anti-Reflex 2, глубокоматовая, подготовка Q3 | Tikkurila F497 «Paper» | 2,8 м² |

### Примечания


1. Размеры — в мм от чистовых поверхностей стен; условные обозначения и общие указания — лист 3.
2. Картины и зеркала крепить к основанию по паспорту изделия (закладные и анкеры — в перечне скрытых работ); крест — ось центра предмета.

| | | | | | | |
|---|---|---|---|---|---|---|
| | | | | | Проект: Четырёхкомнатная квартира | М 1:20 |
| | Лист | № док. | Подпись | Дата | | |
| Дизайнер | Кырлан А.С. | | | 04.11.26 | Развёртки стен. Гардеробная 1 (пом. 12) | Стадия: П; Лист: 89; Листов: 120 |


## Развёртка стены А

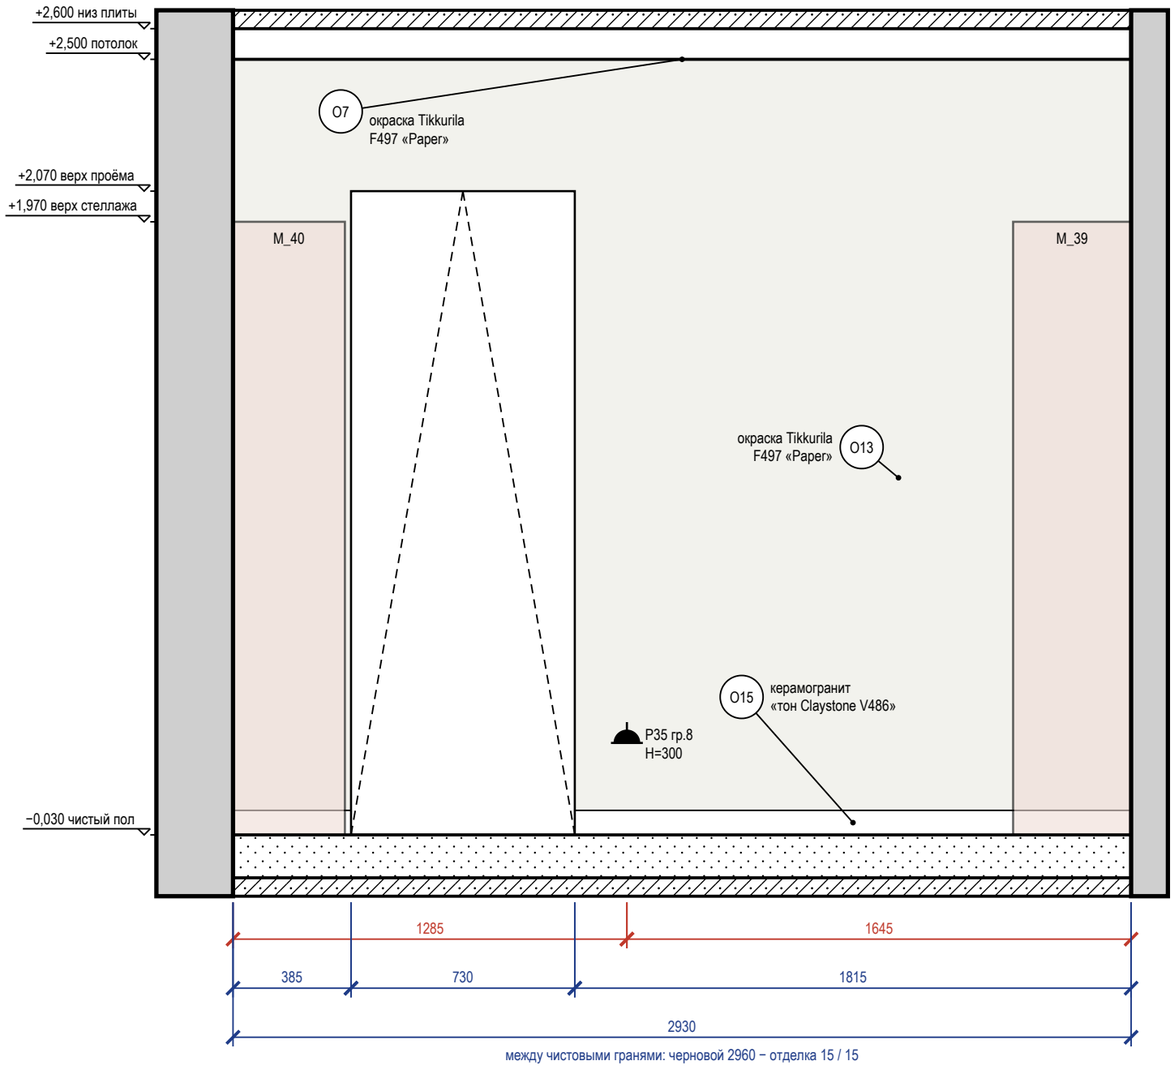


## Развёртка стены Б

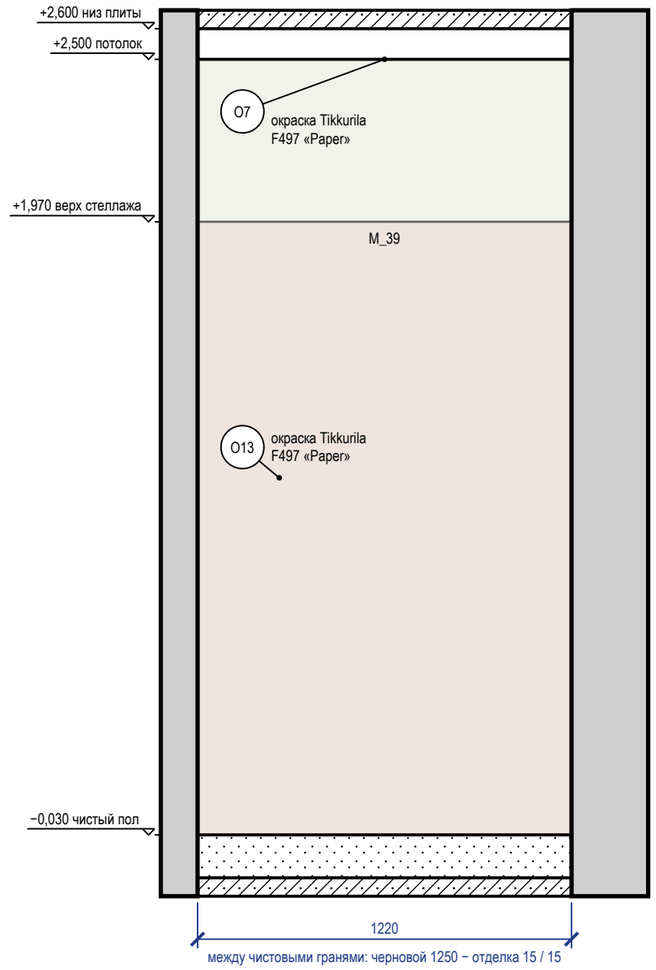


### Схема развёрток (М 1:100)

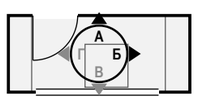


### Ведомость отделки (на листе)

| Марка | Поверхность | Материал, изделие | Цвет, код | Кол. |
|---|---|---|---|---|
| O7 | потолок | окраска, Tikkurila Luja 7, матовая, подготовка Q3 | Tikkurila F497 «Paper» | 3,7 м² |
| O13 | стены | окраска, Tikkurila Luja 7, шелковисто-матовая, подготовка K3 | Tikkurila F497 «Paper» | 9 м² |
| O15 | плинтус | керамогранит, аналог: плинтус из керамогранита пола, подрезка 80 мм, верхняя кромка с запилом 45° | #B8AFA5 «тон Claystone V486» | 2,2 м |


### Примечания

1. Размеры — в мм от чистовых поверхностей стен; условные обозначения и общие указания — лист 3.


| | | | | | | |
|---|---|---|---|---|---|---|
| | | | | | Проект: Четырёхкомнатная квартира | М 1:20 |
| | Лист | № док. | Подпись | Дата | | |
| Дизайнер | Кырлан А.С. | | | 04.11.26 | Развёртки стен А, Б. Балкон 1 (пом. 13) | |
| | | | | | Стадия: П | Лист: 90 / Листов: 120 |

выпуск 04.11.2026 № b23f08ad9b · стр. 90 из 120


## Развёртка стены В

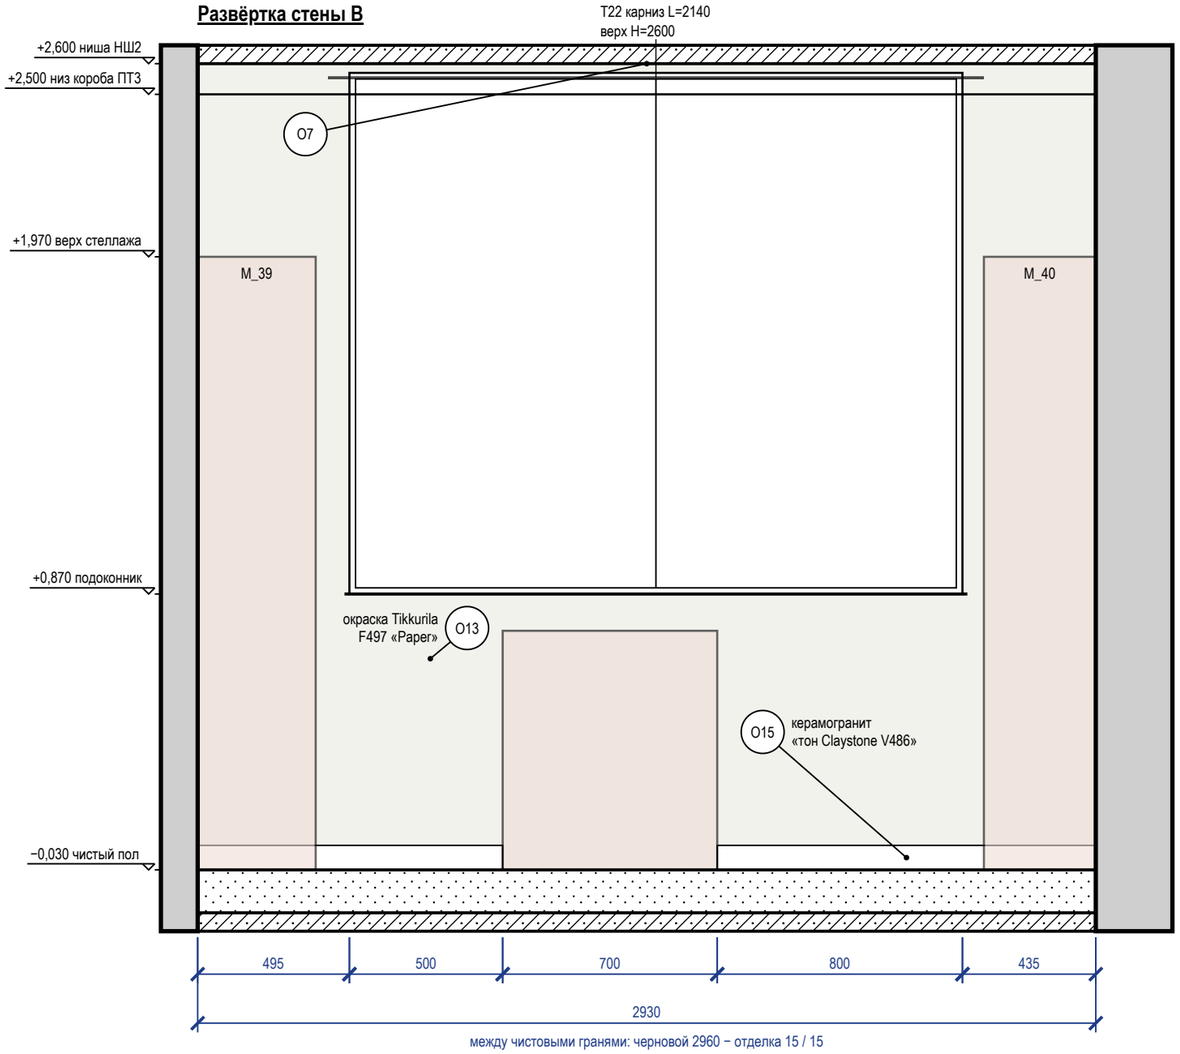


## Развёртка стены Г

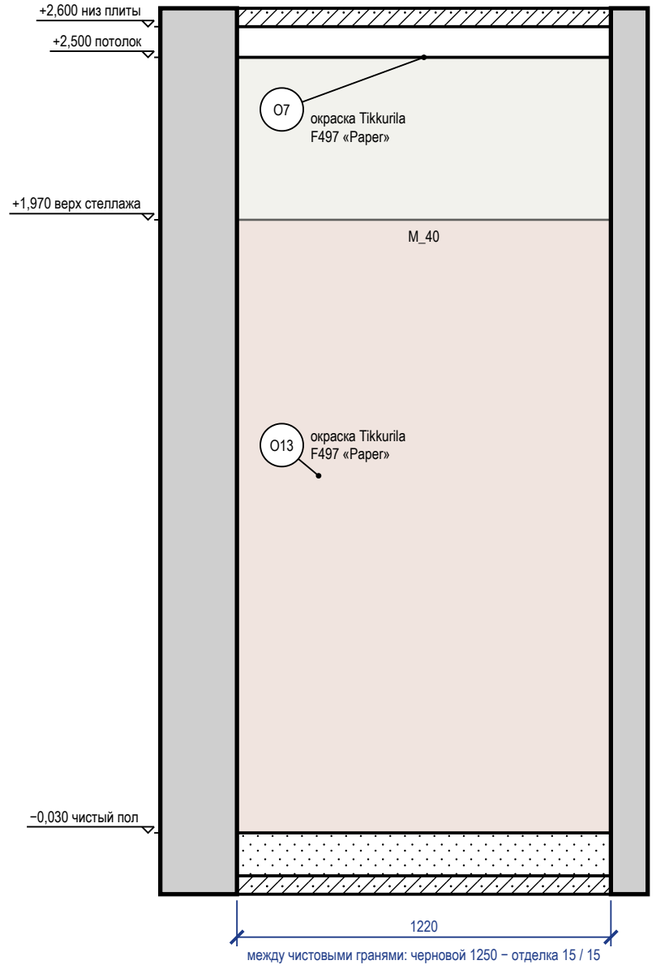


### Схема развёрток (М 1:100)

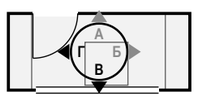


### Ведомость отделки (на листе)

| Марка | Поверхность | Материал, изделие | Цвет, код | Кол. |
|---|---|---|---|---|
| О7 | потолок | окраска, Tikkurila Luja 7, матовая, подготовка Q3 | Tikkurila F497 «Paper» | 3,7 м² |
| О13 | стены | окраска, Tikkurila Luja 7, шелковисто-матовая, подготовка К3 | Tikkurila F497 «Paper» | 7,4 м² |
| О15 | плинтус | керамогранит, аналог: плинтус из керамогранита пола, подрезка 80 мм, верхняя кромка с запилом 45° | #B8AFA5 «тон Claystone V486» | 2,2 м |

### Примечания

1. Размеры — в мм от чистовых поверхностей стен; условные обозначения и общие указания — лист 3.
2. Карнизы (шины) — по ведомости текстиля декоратора: длина L и верх H на развёртке — те же числа, что в ведомости; крепление — до окраски потолка.

| | | | | |
|---|---|---|---|---|
| | Лист | № док. | Подпись | Дата |
| Дизайнер | Кырлан А.С. | | | 04.11.26 |

Проект: Четырёхкомнатная квартира — М 1:20

Развёртки стен В, Г. Балкон 1 (пом. 13)

| Стадия | Лист | Листов |
|---|---|---|
| П | 91 | 120 |

выпуск 04.11.2026 № b23f08ad9b · стр. 91 из 120

Комплект предварительный по пунктам этих таблиц. Пока по пункту нет ответа или решения, показанное на указанном листе — допущение проектировщика, а не утверждённое решение.
Сводка: открытых вопросов — 27 (из них ждут факта объекта — 15: контрольного обмера, обследования или документа); конфликтов между разделами — 1; изменений в реестре — 20, из них без подписи — 7; разделов, не сданных к выпуску, — 1.

## Открытые вопросы и принятые допущения

| № | Формулировка | Вид | Кто решает | Если решения нет | Лист, где это проявляется |
|---|---|---|---|---|---|
| К-1 | Окно детской 2 (поз. 9) на наружной стене В: привязки 1580…3080 в источниках нет — в экспликации скана окна этой комнаты не показано. Это допущение проектировщика, центровка, а не замер: окно 1500 мм поставлено примерно по центру наружного участка стены В (по контуру 8030–10610 по оси Х, центр 9320; окно 8540–10040, центр 9290). Размер 1500×1600 и подоконник 800 мм взяты из исходной записи окна, источник размера в данных не указан. Из допущения следует конфликт со стояками Ст К1-2 и Ст В1-2 (9400; 6300) и (9560; 6300): они попадают в проём окна вместе с коробом и люком (конфликт Кф-1, вопрос К-15). Нужен контрольный обмер эркера: положение, размер и подоконник окна, затем осей стояков. | Непонятно<br>Ждёт: обмера | Архитектор-планировщик | Остаётся принятое положение окна как допущение, не замер. Конфликт со стояками Кф-1 не снят: радиатор под окном, шторы и короб со стояками на этом месте не совмещаются. | л. 6 — План планировки от заказчика |
| К-3 | Несущие стены не определены (нет плана БТИ и техзаключения): до их получения демонтаж не планируется. Нужно: запросить проект дома и поэтажный план БТИ, установить серию дома; несущие стены и допустимость вмешательства определяет техническое заключение специализированной организации. Тип дома (монолит) и перекрытие (монолитная плита 220 мм) в данных приняты допущением: источника — проекта дома, плана БТИ, обследования — в материалах объекта нет; материал основания стен и перекрытия определит тот же документ или обследование. | Отсутствует<br>Ждёт: документа, обследования | Архитектор-планировщик | Исходных данных нет: на листе нет решения по этому пункту или оно условное; лист предварительный. | полный альбом |
| К-4 | Гостиная (поз. 11): мебели в модели нет, расстановка ждёт решения заказчика. Отделка, потолок, свет, розетки и декор выполнены; акцентная стена А L481 возвращена (см. К-7); картина ДК20, ваза ДК21 и подсветка картины — предложение конвейера (ИЗ-7). Площадь по модели 14,55 м² (≈17 м² по реконструкции контура — снимет контрольный обмер). | Отсутствует<br>Ждёт: решения | Дизайнер интерьера | Исходных данных нет: на листе нет решения по этому пункту или оно условное; лист предварительный. | л. 16 — План размещения мебели и оборудования |
| К-5 | Гардеробная 1 (поз. 12) в натуре трапеция 2320/2132/1400, в модели прямоугольник той же площади: нужен контрольный обмер углов. | Непонятно<br>Ждёт: обмера | Архитектор-планировщик | Остаётся значение, принятое по исходным данным; оно не подтверждено, лист предварительный. | л. 6 — План планировки от заказчика |
| К-6 | Розетка Р7 (стиральная машина, ванная комната) стоит в 72 мм от угла при норме от 150 мм. Р7 возвращена на прежнее место: стена В, смещение 2543 мм, высота 949 мм — норма ПУЭ 6.6.30 (не выше 1 м) выполнена, флага решения нет; конвейер уходил от угла переносом на 2242 мм и высоту 1250 мм, что нарушало ПУЭ 6.6.30, — этот перенос отменён. Нужно решение автора: сдвинуть машину и розетку от угла или принять 72 мм. Норма для розеток ванной (ПУЭ 7.1.48 против BS 7671) решена: ИЗ-19. | Спорно<br>Ждёт: решения | Инженер-электрик | Р7 остаётся на 2543 мм вдоль стены и 949 мм по высоте, в 72 мм от угла: замечание открыто. | л. 43 — План розеток и электровыводов |
| К-7 | Акцент L481 занимает больше порога 15 % площади поверхностей на акцентной стене А Гостиной — 16 % (проверка по доле акцента, замечание открыто намеренно). Красить плоскость целиком (нужна поддержка в модели), перенести акцент на предметы (в Гостиной они уже есть — ДК20, ДК21, ИЗ-7) или принять 16 %. Для Зала решение принято: 18 % приняты автором (ИЗ-15). | Спорно<br>Ждёт: решения | Колорист-комплектатор | Остаётся акцентная стена L481 в Гостиной, доля 16 % выше порога 15 %; замечание открыто. | л. 14, 15 — Колерная карта |
| К-8 | Графы «Пров.» и «Н. контр.» в штампе пусты: их заполняет человек, подписи проверяющего и нормоконтролёра автор проекта не ставит; для выдачи нужны разные подписанты, отличные от разработчика. Решение автора (ИЗ-18): графы остаются пустыми, комплект предварительный. | Отсутствует<br>Ждёт: решения | Нормоконтролёр | графы остаются пустыми; комплект предварительный, не проверен независимо | л. 3 — Список листов |
| К-10 | Прямые углы помещений с кухней, санузлами, гардеробными и встроенной мебелью по скану не подтверждены (скос стен приведён к ступеням): ванная комната, тёмная комната, детская 1, коридор, кухня, прихожая-коридор, гардеробная 2, детская 2, гардеробная 1, балкон 1. Нужен контрольный обмер: длины сторон, обе диагонали, отклонения углов от 90° у стен под встроенную мебель и плитку; только после него отмечаются углы 90°. | Отсутствует<br>Ждёт: обмера | Архитектор-планировщик | Исходных данных нет: на листе нет решения по этому пункту или оно условное; лист предварительный. | л. 6 — План планировки от заказчика |
| К-12 | Состав подрядчиков и поставщиков (кто покупает и кто монтирует радиаторы, подоконники, двери, розетки) от заказчика не получен. Принята типовая схема частного ремонта (ИЗ-17): материалы и оборудование покупает заказчик по спецификациям проекта, монтаж ведёт подрядная бригада, приёмку скрытых работ ведёт автор. Схема уточняется договором подряда: нужен договор или состав подрядчиков и поставщиков от заказчика. | Отсутствует<br>Ждёт: решения | Прораб-координатор | остаётся типовая схема: покупает заказчик, монтирует подрядная бригада, скрытые работы принимает автор; закрепление за конкретными подрядчиками не подтверждено | л. 3 — Список листов |
| К-13 | Детская 2: рабочий стол M_35 у стены Б получает боковой свет от окна справа от сидящего; для правши лучше свет слева подтвердить, кто сидит за столом (правша или левша), иначе решить зеркальной расстановкой (нужен перенос двери) либо второй лампой слева. | Спорно<br>Ждёт: решения | Дизайнер интерьера | Остаётся вариант, показанный на листе; он не утверждён, лист предварительный. | л. 16 — План размещения мебели и оборудования |
| К-14 | Из чего стены под навесными шкафами — Ванная комната (стена Б, M_07), Кухня (стена А, M_23, M_24, M_25), Гардеробная 2 (стена В, M_32)? Проекта дома нет, на скане материал и толщина не читаются. Нужно обследование: материал основания определяет крепёж (анкер по бетону, закладная в ГКЛ). До ответа материал в данных не указан, замечание открыто намеренно. | Отсутствует<br>Ждёт: вскрытия | Мебельщик | Исходных данных нет: на листе нет решения по этому пункту или оно условное; лист предварительный. | л. 8 — Кухня (пом. 6). Монтажная схема<br>л. 9 — Кухня (пом. 6). Монтажная схема<br>л. 10–12 — Шкафы. Монтажная схема |
| К-15 | Стояки Ст К1-2 и Ст В1-2 (в данных (9400; 6300) и (9560; 6300), короб и люк) попадают в проём окна Детской 2 по стене В (8540–10040): совместить с радиатором под окном и шторами нельзя. Привязку осей стояков от двух стен никто не замерял; в Санузле они не стоят, выпуск унитаза С_06 от этого положения — 2,4 м. Нужен контрольный обмер стояков и окна, затем решение: сдвинуть окно, перенести радиатор или обойти короб. | Спорно<br>Ждёт: обмера, затем решения | Инженер ВК (вода, канализация) | Остаются принятые положения окна и стояков без замера; радиатор под окном, шторы и короб со стояками на этом месте не совмещаются. | л. 22 — План выводов сантехники<br>л. 23 — Схема разводки водопровода и канализации<br>л. 6 — План планировки от заказчика |
| К-17 | Ведущий цвет — Paper F497 на стенах и потолке — занимает больше 80 % площади поверхностей в Тёмной комнате (87 %), Гардеробной 2 (89 %), Гардеробной 1 (86 %) и Балконе 1 (85 %): второй цвет почти не читается. Это цвета автора проекта. Принять как есть или задать этим помещениям второй цвет. | Спорно<br>Ждёт: решения | Колорист-комплектатор | Остаются цвета автора: стены и потолок в Paper F497, доля ведущего цвета 85–89 %. | л. 14, 15 — Колерная карта |

| | | | | | |
|---|---|---|---|---|---|
| | | | | | Проект: Четырёхкомнатная квартира |
| | Лист | № док. | Подпись | Дата | Открытые вопросы, принятые допущения и конфликты. Лист 1 из 5 |
| Дизайнер | Кырлан А.С. | | | 04.11.26 | |

| Стадия | Лист | Листов |
|---|---|---|
| П | 92 | 120 |

## Открытые вопросы и принятые допущения (продолжение)

| № | Формулировка | Вид | Кто решает | Если решения нет | Лист, где это проявляется |
|---|---|---|---|---|---|
| К-18 | Вытяжка M_24 встроена в навесной модуль на отметке 1550 мм: её низ над электрической варочной панелью 610 мм, а фартук 650 мм при практике 450–600 мм. Модель вытяжки не выбрана, паспорта нет, допустимая высота над варочной неизвестна. Поднять модуль M_24 (и соседние M_23, M_25 — на единую отметку), либо выбрать вытяжку, допускающую 610 мм по паспорту. | Спорно<br>Ждёт: данных закупки, затем решения | Мебельщик | Остаётся модуль на отметке 1550 мм; низ вытяжки 610 мм над панелью, меньше 650 мм; допустимость высоты не подтверждена. | л. Д_14, Д_15 — Д_14 Кухня (пом. 6). Развёртка гарнитура |
| К-19 | Привязка угла помещения «Гостиная» (поз. 12 скана; в примечании проекта названо «зал») принята в точке (10670; 3470) мм — это допущение, не замер: по пиксельной привязке скана угол может лежать примерно на 700 мм левее. От этой точки по оси X отсчитываются Гостиная и Гардеробная 1, по ней же проходит стена Детской 2 со стороны Гостиной. Нужен контрольный обмер: расстояние от опорной стены до этого угла. | Непонятно<br>Ждёт: обмера | Архитектор-планировщик | Остаётся угол в точке (10670; 3470) как допущение: размеры правой части на листах — расчётные, возможен сдвиг до ≈700 мм; мебель, свет и розетки там привязаны к принятым координатам. | л. 6 — План планировки от заказчика |
| К-20 | Наружные скошенные стены (в натуре под 45°) заменены на планах ступенями: движок описывает только ортогональную геометрию. Гостиная — три ступени, площадь по модели 14,55 м² против ≈17 м² по реконструкции контура; Гардеробная 1 — прямоугольник 1400×2230 вместо трапеции 2320/2132/1400 той же площади (К-5). Углы и длины скосов на листах не показаны, площади у скошенных стен условные (К-10). Принять ступени как условность до обмера или передать скосы обмером и отдельным чертежом. | Спорно<br>Ждёт: решения | Архитектор-планировщик | Остаются ступени вместо скоса: фактическая форма наружных стен Гостиной и Гардеробной 1 на листах не показана, размеры вдоль скоса брать по обмеру на месте. | л. 6 — План планировки от заказчика<br>л. 16 — План размещения мебели и оборудования |
| К-21 | Все размеры сняты с размерных цепочек растрового скана заказчика, контрольного обмера нет. Площади помещений и «Общая площадь 102,67 м²» в штампе каждого листа — расчётные по модели, не обмерные: итог зависит от ступеней вместо скоса (К-20) и принятого угла Гостиной (К-19). Названия и номера помещений со сканом не сверены (общая комната назначена решением автора, ИЗ-13). Толщины стен приняты допущением: наружные 250 мм, внутренние 120 мм, источника (обмер, проект дома) нет. Всё, что на листах выглядит как замер, снято со скана. | Отсутствует<br>Ждёт: обмера | Архитектор-планировщик | Размеры и площади остаются ориентировочными; штамп печатает «Общая площадь 102,67 м²» как расчётную величину, не подтверждённую обмером; до обмера не заказывать материалы и изделия по размерам листов. | л. 3 — Список листов<br>л. 6 — План планировки от заказчика |
| К-22 | Окно Гостиной (пом. 11) на стене В, часть 2: остекление показано по обмерному скану, размеры 1500×1600 мм и подоконник 900 мм приняты типовыми, не замерены. Нужен контрольный обмер окна: положение, ширина, высота, подоконник. | Непонятно<br>Ждёт: обмера | Архитектор-планировщик | Остаются типовые размеры окна 1500×1600 мм, подоконник 900 мм; на плане они напечатаны как принятые, не замеренные. | л. 6 — План планировки от заказчика |
| К-23 | Две розетки выше 1 м от пола остаются предложением проектировщика, решения автора нет: Р21 (вытяжка M_24, 2200 мм, в модуле за съёмной панелью, Кухня) и Р27 (слаботочный щит ЩС, 1600 мм, Прихожая-коридор). Основание — назначение розетки; автор высоту не подтверждал; основание записано в самой позиции (знак «**» у марки, примечание листа). Норма (ПУЭ, п. 6.6.30) — не выше 1 м. Подтвердить высоты или опустить розетки. | Спорно<br>Ждёт: решения | Инженер-электрик | Высоты остаются как на листе, решение автором не подтверждено. | л. 43 — План розеток и электровыводов полный альбом |
| К-24 | Высота потолка 2700 мм принята: источника (замер, проект дома) в материалах объекта нет. От неё зависят вертикальные размеры альбома: развёртки, шкафы и встроенная мебель, плитка, потолки, объёмы работ. Замерить высоту на объекте в каждом помещении. | Непонятно<br>Ждёт: обмера | Архитектор-планировщик | Высота 2700 мм остаётся принятой, не замеренной: вертикальные размеры листов и объёмы работ ориентировочные; встроенную мебель и плитку по высоте не заказывать до замера. | л. 6 — План планировки от заказчика |
| К-25 | Разрешённая мощность 15 кВт принята, технических условий в материалах объекта нет; расчётная мощность 11,2 кВт. Сверить с техническими условиями. | Непонятно<br>Ждёт: документа | Инженер-электрик | Разрешённая мощность 15 кВт остаётся принятой, не подтверждённой техническими условиями: вводной аппарат и группы щита предварительные. | л. 41, 42 — Однолинейная схема щита |
| К-26 | Артикулы изделий отделки не выбраны. Инженерная доска (пом. 1, 3, 4, 6, 8, 9, 11, 12), керамогранит пола (пом. 2, 5, 7, 10, 13), керамогранит стен санузла и ванной (пом. 2, 10) и фартука кухни (пом. 6), плинтус МДФ (пом. 1, 3–9, 11, 12), плинтус из керамогранита (пом. 13) и краска акцентных стен (пом. 1, 11) заданы характеристиками — «аналог по характеристикам», кода изделия производителя нет. Цвет керамогранита назван тоном по колерной карте (J484, F497, V486), но тон — не артикул изделия. Артикул выбирается при закупке: выбрать изделия, вписать артикулы в ведомость отделки и спецификации, цвет и тон принять по образцу из партии. Количество к заказу и упаковки — расчётные, по номинальным размерам, до выбора изделия. | Отсутствует<br>Ждёт: данных закупки, затем решения | Отделочник | материалы остаются описанными характеристиками; заказ по спецификации и подсчёт упаковок — только после выбора изделий | л. 51 — Раскладка плитки. Планы полов<br>л. 52 — Раскладка плитки. Фартук кухни<br>л. 32 — Раскладка плитки. Ванная комната. Развёртки стен<br>л. 33 — Раскладка плитки. Санузел. Развёртки стен<br>л. 50 — План покрытий пола<br>л. С1, С2, С3 — С1–С3 Ведомость отделки помещений<br>л. 14, 15 — Колерная карта<br>л. С4, С5 — С4–С5 Спецификация отделочных материалов<br>полный альбом |
| К-27 | Модели встраиваемой техники кухни не выбраны: холодильник (M_19), духовой шкаф (M_21) и посудомоечная машина (M_26) заданы описанием «аналог по характеристикам» — без производителя, серии и кода. Размеры ниш и вентзазоры взяты по типовой схеме на 600 мм, а не по паспорту модели: у разных изготовителей они расходятся, и модуль, сделанный по типовой нише, может не принять выбранную технику. Вытяжка M_24 — отдельный вопрос К-18. Нужно: выбрать модели, получить монтажные схемы изготовителей и сверить ниши модулей, вентиляцию и подключение до заказа гарнитура. | Отсутствует<br>Ждёт: данных закупки, затем решения | Мебельщик | ниши остаются по типовой схеме на 600 мм, не подтверждённой паспортом модели; модули кухни не заказывать до выбора техники | л. Д_14, Д_15 — Д_14 Кухня (пом. 6). Развёртка гарнитура<br>л. 8 — Кухня (пом. 6). Монтажная схема |
| К-28 | Санузел (пом. 10): унитаз С_06 при положении стояков по данным (К-15) имеет выпуск 3600 мм до стояка К1 и 2357 мм до стояка Ø110 по прямой; вход в санузел — только из Детской 2. Длинный выпуск требует нормативного уклона по всей длине (СП 30.13330) — подъёма пола санузла (подиум) или насосной установки. Решить: принять длинный выпуск с подиумом/насосом, перенести унитаз ближе к стояку или перепланировать санузел — после контрольного обмера стояков (К-15). | Спорно<br>Ждёт: решения | Инженер ВК (вода, канализация) | выпуск С_06 остаётся 3600 мм: раскладка санузла и высота пола не утверждены, разводку канализации не выполнять до решения | л. 22 — План выводов сантехники<br>л. 16 — План размещения мебели и оборудования<br>л. 6 — План планировки от заказчика |

| | | | | | |
|---|---|---|---|---|---|
| | | | | | Проект: Четырёхкомнатная квартира |
| | Лист | № док. | Подпись | Дата | Открытые вопросы, принятые допущения и конфликты. Лист 2 из 5 |
| Дизайнер | Кырлан А.С. | | | 04.11.26 | |

| Стадия | Лист | Листов |
|---|---|---|
| П | 93 | 120 |

## Открытые вопросы и принятые допущения (продолжение)

| № | Формулировка | Вид | Кто решает | Если решения нет | Лист, где это проявляется |
|---|---|---|---|---|---|
| К-29 | Мойка кухонная C_05 (пом. 6 «Кухня»), выпуск К1-5 Ø50: в полу не помещается: врезка + перепад 202 (10,10 м × 20 мм/м) + Ø50 + слой над трубой 45 = 307 мм при пироге 170 мм. Решить: (а) подиум или подъём пола на 140 мм (ступень на входе — порог); (б) прибор ближе к стояку Ст К1-2; (в) насосная установка (КНС) у прибора — по паспорту, требует согласования. Решение меняет кухню (модули, цоколь, точки ЭОМ) — за автором с заказчиком. | Спорно<br>Ждёт: решения | Инженер ВК (вода, канализация) | выпуск К1-5 и кухню в части мойки не выполнять до решения; остальное — по листам | л. 23 — Схема разводки водопровода и канализации<br>л. 22 — План выводов сантехники |
| К-30 | Посудомоечная машина ОБ_03 (пом. 6 «Кухня»), выпуск К1-6 Ø50: в полу не помещается: врезка + перепад 152 (7,60 м × 20 мм/м) + Ø50 + слой над трубой 45 = 257 мм при пироге 170 мм. Решить: (а) подиум или подъём пола на 90 мм (ступень на входе — порог); (б) прибор ближе к стояку Ст К1-2; (в) насосная установка (КНС) у прибора — по паспорту, требует согласования. Решение меняет кухню (модули, цоколь, точки ЭОМ) — за автором с заказчиком. | Спорно<br>Ждёт: решения | Инженер ВК (вода, канализация) | выпуск К1-6 и кухню в части мойки не выполнять до решения; остальное — по листам | л. 23 — Схема разводки водопровода и канализации<br>л. 22 — План выводов сантехники |
| К-31 | Гостиная (пом. 11, 14,55 м²) в данных без двери и проёма: со всех сторон глухие стены (к детской 1 — стена А, к детской 2 — стена Г, к гардеробной 1 — стена Б), единственная дверь Д-4 ведёт из неё в гардеробную 1, у которой другого выхода нет — два помещения недостижимы из квартиры, при этом в них заведены розетки, свет, LAN и Wi-Fi. По скану внутренней стала стена Б детской 2 на участке 3530…5010 — возможно, там проём; но на этой стене утверждённая расстановка детской 2 (стеллаж M_37, стол M_35, выключатель S18 — ИЗ-1, ИЗ-2). Нужно: выяснить у заказчика вход в гостиную (из детской 2, из детской 1 или новый проём из коридора через перепланировку) и подтвердить обмером; до ответа дверь в данные не вносится. | Отсутствует<br>Ждёт: обследования, затем решения | Архитектор-планировщик | гостиная и гардеробная 1 недостижимы: отделку, потолок, ЭОМ и мебель в них не выполнять; если вход — через детскую 2, расстановку детской 2 (ИЗ-1, ИЗ-2) пересматривать | л. 6 — План планировки от заказчика<br>л. 34 — План размещения дверей<br>л. 16 — План размещения мебели и оборудования |

## Конфликты между разделами

| № | Формулировка | Разделы | Статус | Кто решает | Если решения нет | Лист, где это проявляется |
|---|---|---|---|---|---|---|
| Кф-1 | Стояки Ст К1-2, Ст В1-2 с коробом и люком попадают в проём окна Детской 2 (стена В, 8540–10040): положение стояков и окна не замерено; вопрос К-15. | ВК; архитектура (окно Детской 2) | Открыт, круг 1 | Инженер ВК (вода, канализация) | Положение окна — допущение, стояков — по скану без привязки; пока их не замерили, окно, радиатор под ним и короб со стояками на листах не согласованы. | л. 22 — План выводов сантехники<br>л. 23 — Схема разводки водопровода и канализации |

## Изменения проекта после выпуска листов (реестр изменений)

| № | Дата | Лист | Было | Стало | Кто решил, подпись |
|---|---|---|---|---|---|
| ИЗ-1 | 05.10.2026 | л. 16 — План размещения мебели и оборудования | Окно Детской 2 на стене Б (смещение 900). Стол M_35 1400×650, стена Б, смещение 1000; кресло M_36 (9300; 4950); стеллаж M_37 1200×2100, стена В, смещение 960. | Окно на наружной стене В (1580…3080; положение — допущение, центровка, не замер). Стол M_35 1400×650 (размер и допуск глубины «Г 600–700» прежние), стена Б, смещение 1500; кресло M_36 (9150; 5450); стеллаж M_37 1200×2100 (размер прежний), стена Б, смещение 120. Основания. Стеллаж: на стене В теперь окно, прежнее место перекрывает проём; на стене Б он стоит в углу А/Б. Стол: перенесён вслед за окном на стену Б без изменения размера; при 650 мм край стола заходит на 20 мм в проекцию проёма окна — это не нарушение, принято автором 05.10.2026 (вопрос К-16 закрыт). Вместе с окном изменились: направление паркета в Детской 2 (по оси X → по оси Y, вдоль света от окна), портьеры и римская штора T16, T17 (длина, карниз). Декор: спатифиллум ДК16 перенесён с (9900; 6100) на (10200; 4300), основание в данных не записано. Окно, стол M_35, кресло M_36, стеллаж M_37, портьеры T16, T17, декор ДК16 и направление паркета помечены знаком предложения. | Утверждено: Кырлан А.С., автор проекта, 05.10.2026 — утверждены положение и размеры мебели «Детской 2»: стол M_35 1400 × 650 (заход края стола на 20 мм в проекцию проёма окна принят), кресло M_36, стеллаж M_37 1200 × 2100. Не утверждены (допущение или предложение): положение окна, портьеры T16 и T17, декор ДК16, направление паркета. Предложил: решение автора проекта, оформлено исполнителем по его поручению (запись внесена конвейером). |
| ИЗ-2 | 05.10.2026 | л. 43 — План розеток и электровыводов<br>л. 45 — План освещения<br>л. 47 — Управление светильниками<br>л. 46 — Техническое задание на подбор светильников | Детская 2: общий свет L15 (шесть спотов), выключатель S14 (L15 и свет санузла). Бра и отдельных линий у кровати и у стола не было. | Добавлены: бра Св63 у изголовья кровати M_33 (стена А, смещение 510, высота 1400 мм, 6 Вт, 2700 K, линия L21) и выключатель S17 (стена А, смещение 1050, высота 900 мм); бра Св67 над рабочим столом M_35 (стена Б, смещение 2200, высота 1300 мм, 7 Вт, 3000 K, линия L22) и выключатель S18 (стена Б, смещение 1410, высота 900 мм). S18 стоял на смещении 1350 мм и оказывался за стеллажом M_37 1200×2100: стеллаж возвращён к прежнему размеру, выключатель перенесён в просвет между стеллажом и столом. Заказчик бра не заказывал, основание в данных не записано; позиции помечены как предложение проектировщика. | Утверждено: Кырлан А.С., автор проекта, 05.10.2026 — утверждён перенос выключателя S18 в просвет между стеллажом M_37 и столом M_35 (стеллаж прежнего размера 1200 × 2100). Не утверждены (предложение проектировщика): бра Св63 и Св67, выключатели S17 и S18 как позиции, линии L21 и L22. Предложил: решение автора проекта, оформлено исполнителем по его поручению (запись внесена конвейером). |
| ИЗ-3 | 05.10.2026 | л. 45 — План освещения<br>л. 46 — Техническое задание на подбор светильников | Санузел: общий свет L12 (спот Св51), света у зеркала не было. | Добавлен светильник Св64 над зеркалом ДК17 (стена Б, смещение 600, высота 1950 мм, 8 Вт, 3000 K, IP44, драйвер встроен, линия L12, группа 4). Основание: (свет у зеркала в санузле). Заказчик светильник не заказывал; решение исполнителя, знак «**» у Св64 остаётся. | Утверждено: исполнитель по поручению Кырлана А.С., 05.10.2026. Предложил: исполнитель. |



| | | | | | | | |
|---|---|---|---|---|---|---|---|
| | | | | | Проект: Четырёхкомнатная квартира | | |
| | Лист | № док. | Подпись | Дата | Открытые вопросы, принятые допущения и конфликты. Лист 3 из 5 | Стадия | Лист | Листов |
| Дизайнер | Кырлан А.С. | | | 04.11.26 | | П | 94 | 120 |

## Изменения проекта после выпуска листов (реестр изменений) (продолжение)

| № | Дата | Лист | Было | Стало | Кто решил, подпись |
|---|---|---|---|---|---|
| ИЗ-4 | 05.10.2026 | л. 47 — Управление светильниками<br>л. 46 — Техническое задание на подбор светильников | Зал: выключатель S2 (лента в карнизе L3) без светорегулятора, сценариев света нет. | В S2 добавлен светорегулятор (тип TE, под диммируемую ленту); записаны четыре сценария света: «Вечер» (L1 0 %, L2 100 %, L3 50 %), «Гости» (100/100/100 %), «Кино» (0/0/20 %), «Уборка» (100/100/0 %). Основание: (гостиная с тремя и более группами света — сценарий; в Зале L1–L3) и (промежуточный уровень — группе на светорегуляторе). Уровни выбрал исполнитель, заказчик их не задавал; знак «**» у S2 остаётся. Сценарии и диммер записаны для Зала; в Гостиной их нет. | Утверждено: исполнитель по поручению Кырлана А.С., 05.10.2026. Предложил: исполнитель. |
| ИЗ-5 | 05.10.2026 | л. 41, 42 — Однолинейная схема щита<br>л. 43 — План розеток и электровыводов полный альбом | Розетки Гостиной Р36–Р38 — в группе 9 «розетки фартука кухни». Щит ЩРВ-П-54 на 54 модуля, занято 42. | Новая группа 19 «розетки гостиной»: автомат С16, УЗО 30 мА типа А, кабель ВВГнг(А)-LS 3×2,5, 1,0 кВт, длина линии 30 м (оценка, не замер). Щит ЩРВ-П-72 на 72 модуля, занято 44. Основание щита: при 44 занятых модулях резерв ЩРВ-П-54 составил бы 10 модулей (18,5 %) — меньше 20 %. Основание группы 19: (не больше 12 гнёзд на группу 2,5 мм²; практика): с Р36–Р38 в группе 9 было бы 14 гнёзд, осталось 8. Знак «**» у щита и Р36–Р38 остаётся. | Не утверждено: подписи нет. решение исполнителя; на утверждение А. С. Кырлана |
| ИЗ-6 | 05.10.2026 | л. 34 — План размещения дверей<br>л. 16 — План размещения мебели и оборудования | Гардеробная 1: дверь в Гостиную, проём 1420 мм по скану, полотно распашное 1420 мм. | Полотно раздвижное, две створки по 710 мм по накладной направляющей; проём 1420 мм прежний. Основание: распашное полотно 1420 мм в помещении 1400×2230 задевало стеллаж M_38. Заказчик замену не заказывал; решение исполнителя, знак предложения у двери остаётся. | Утверждено: исполнитель по поручению Кырлана А.С., 05.10.2026. Предложил: исполнитель. |
| ИЗ-7 | 05.10.2026 | полный альбом<br>л. 14, 15 — Колерная карта<br>л. 45 — План освещения<br>л. 47 — Управление светильниками | Гостиная: акцентная стена А в L481 (finish.accent); предметов декора и подсветки картины не было; выключатель S16 одноклавишный (L19). | Конвейер заменял акцентную стену предметами и ради порога снял её; решением от 05.10.2026 акцентная стена А возвращена (доля 16 % выше порога 15 %, замечание открыто, К-7). Предметы оставлены как предложение: картина ДК20 (стена Г, 800×600), ваза ДК21, подсветка картины Св65, Св66 (линия L20), вторая клавиша S16, подсветка помечена как предложение проектировщика. Нужны ли предметы при акцентной стене — решает автор. | Не утверждено: подписи нет. ИИ-конвейер, на утверждение А. С. Кырлана |
| ИЗ-8 | 05.10.2026 | л. 6 — План планировки от заказчика<br>л. 43 — План розеток и электровыводов<br>л. 45 — План освещения | Наружный контур: ступени по осям 14780, 7710, 6540, 7970 мм. Прихожая-коридор: розетка Р27 на стене Г, смещение 1990; ИП5 (5600; 3800). Коридор: ИП3 (8500; 3200), выключатель S4 смещение 870. Детская 1: Св20, Св25 по X 14450. Ванная: Св13 по X 7700, дверь смещение 100. Детская 2: Р33 смещение 3140 мм. | Ступени контура 14840, 7770, 6600, 8030 мм (+60 мм): приведены к крайним граням помещений модели (Детская 1, Санузел); после этого окна Гостиной, Детской 1 и Детской 2 лежат на гранях контура. Р27 на стене А, смещение 1750; ИП5 (5500; 4400), ИП3 (8300; 2850). Св20, Св25 по X 14400 и Св13 по X 7600. Дверь ванной смещение 110. Р33 на смещении 1100 мм: прежнее место попало в проём перенесённого окна (ИЗ-1). S4 смещение 880: вслед за дверью ванной (110 вместо 100), зазор от откоса до выключателя прежний, 70 мм. Сдвиги — решение исполнителя; знак «**» у сдвинутых позиций остаётся. | Не утверждено: подписи нет. решение исполнителя; на утверждение А. С. Кырлана |
| ИЗ-9 | 05.10.2026 | л. 43 — План розеток и электровыводов<br>л. 45 — План освещения<br>л. 6 — План планировки от заказчика | Слаботочные точки (5 шт.) без слаботочного щита; точек доступа Wi-Fi не было; параметров щита ЩС в данные проекта не было. | Добавлены: слаботочный щит ЩС (Прихожая-коридор, стена А, смещение 1380, высота 1600 мм), точки доступа AP1 (5500; 5000) и AP2 (13000; 4300), кабель U/UTP кат. 6 у LAN4 и в данные проекта, щит ЩС: глубина 150 мм, пластик, вентилируемый, роутер внутри. Основание: (нет щита) и (ориентир две точки доступа на 102 м²). Заказчик слаботочку в таком составе не заказывал; решение исполнителя, знак «**» у ЩС, AP1, AP2 и LAN4 остаётся. Две точки Wi-Fi и тип щита автор не выбирал. | Не утверждено: подписи нет. решение исполнителя; на утверждение А. С. Кырлана |
| ИЗ-10 | 05.10.2026 | л. 43 — План розеток и электровыводов полный альбом | Кухня: розетка Р21 (вытяжка M_24) на высоте 2200 мм, решение, назначение «вытяжка M_24». | Назначение «вытяжка M_24 (в модуле, съёмная панель)» и признак доступа access: true. Высота 2200 мм прежняя, знак предложения прежний, флаг «решение» снят: решающего нет; высота автором не подтверждена, вопрос К-23. | Не утверждено: подписи нет. решение исполнителя; на утверждение А. С. Кырлана |
| ИЗ-11 | 05.10.2026 | л. 16 — План размещения мебели и оборудования<br>л. 14, 15 — Колерная карта | Марки декора Д1…Д19 (совпадали с префиксом дверей Д). Образцов колерной карты 10. | Марки декора ДК1…ДК19, позиции не менялись. Добавлен образец № 11 (J484, Tikkurila): отдельный выкрас плинтуса коридора и прихожей на МДФ. | Не утверждено: подписи нет. решение исполнителя; на утверждение А. С. Кырлана |
| ИЗ-12 | 24.09.2026 | л. 43 — План розеток и электровыводов полный альбом | В ванной комнате и санузле не было вывода к вентилятору вытяжки и коробки уравнивания потенциалов. | Добавлены выводы к вентиляторам: ЭВ2 (ВР1, ванная комната) и ЭВ5 (ВР3, санузел) — группа 4, высота 2550 мм, IP44, включение с основным светом, таймер выбега в вентиляторе; коробки уравнивания потенциалов КУП1 (ванная комната) и КУП2 (санузел) — высота 300 мм, у входа, вне зон 0–2. Основание: правила проверки (питание вентилятора вытяжки мокрого помещения) и (КУП в помещении с ванной или душем). Заказчик эти позиции не заказывал; решение исполнителя, ЭВ2, ЭВ5, КУП1 и КУП2 со знаком «**». | Утверждено: исполнитель по поручению Кырлана А.С., 05.10.2026. Предложил: исполнитель. |
| ИЗ-13 | 05.10.2026 | л. 16 — План размещения мебели и оборудования<br>л. 6 — План планировки от заказчика | Общая комната квартиры не названа: «Зал» (18,16 м²) или «Гостиная» (14,55 м²); если бы общей считалась «Гостиная», норма 16 м² не выполнялась (вопрос К-9). | Общей комнатой назначен «Зал» (18,16 м²): он больше «Гостиной», проходит норму общей комнаты не менее 16 м² (СП 54.13330.2022, п. 5.11) и по концепции интерьера несёт обеденную группу на шесть персон. «Гостиная» (14,55 м²) остаётся второй жилой комнатой: для неё действует норма спальни 8 м², она выполнена. Названия и номера помещений со сканом по-прежнему не сверены (К-21). | Утверждено: Кырлан А.С., автор проекта, 05.10.2026. Предложил: решение автора проекта, оформлено исполнителем по его поручению. |



| | | | | | |
|---|---|---|---|---|---|
| | | | | | Проект: Четырёхкомнатная квартира |
| | Лист | № док. | Подпись | Дата | Открытые вопросы, принятые допущения и конфликты. Лист 4 из 5 |
| Дизайнер | Кырлан А.С. | | | 04.11.26 | |

| Стадия | Лист | Листов |
|---|---|---|
| П | 95 | 120 |

## Изменения проекта после выпуска листов (реестр изменений) (продолжение)

| № | Дата | Лист | Было | Стало | Кто решил, подпись |
|---|---|---|---|---|---|
| ИЗ-14 | 05.10.2026 | л. 6 — План планировки от заказчика<br>л. 34 — План размещения дверей | Санузел (поз. 10) в эркере соединён только с «Детской 2»: другого входа нет; вход в помещение с унитазом из жилой комнаты расходится с требованием СП 54 (вопрос К-2). | Сохраняется существующее положение: вход в санузел — из «Детской 2», перепланировка с тамбуром не выполняется. Основание: требование СП 54.13330.2022 (формулировка не сверена с первоисточником) не допускает устраивать вход в помещение с унитазом из жилой комнаты; проект нового входа не устраивает, а оставляет существующий. Тамбур отнял бы площадь «Детской 2», а стены до технического заключения считаются несущими (К-3). Существующий вход взят с обмерного скана заказчика, на объекте не проверен (К-21). Это отступление от требования, рассчитанного на новое строительство, принято как существующее положение; проверка по этому пункту остаётся замечанием. | Утверждено: Кырлан А.С., автор проекта, 05.10.2026. Предложил: решение автора проекта, оформлено исполнителем по его поручению. |
| ИЗ-15 | 05.10.2026 | л. 14, 15 — Колерная карта<br>л. 16 — План размещения мебели и оборудования | Зал: акцентная стена А (ТВ-стена, L481) занимает 18 % площади поверхностей при пороге акцента 15 % (вопрос К-7). | Доля акцента 18 % принята: ТВ-стена А красится в L481 целиком, это замысел автора, на предметы акцент не переносится. Порог 15 % практики 60/30/10 превышен сознательно. Акцентная стена «Гостиной» (16 %) этим решением не затронута — вопрос К-7. | Утверждено: Кырлан А.С., автор проекта, 05.10.2026. Предложил: решение автора проекта, оформлено исполнителем по его поручению. |
| ИЗ-16 | 05.10.2026 | л. 3 — Список листов | Состав выдачи не подтверждён: разделы пожарного инженера, акустика, технадзора, слаботочки и допуск ГИПа в сводке ролей числились не сданными (вопрос К-11). | Пожарный инженер, акустик и технадзор в заказ частного ремонта квартиры не входят: роли отмечены в сводке ролей пропущенными, с причиной. Слаботочка входит в состав: выпущен лист «План слаботочных сетей»; отдельная ведомость слаботочки (кабельный журнал, состав слаботочного щита) ролью не сдана и остаётся в таблице несданных разделов. Функции ГИП выполняет автор проекта, графа «ГИП» основной надписи заполнена его фамилией; членство в СРО не проверялось. | Утверждено: Кырлан А.С., автор проекта, 05.10.2026. Предложил: решение автора проекта, оформлено исполнителем по его поручению. |
| ИЗ-17 | 05.10.2026 | л. 3 — Список листов | Матрицы ответственности (делает / поставляет / принимает / хранит) нет; кто покупает и кто монтирует — не определено (вопрос К-12). | Принята типовая схема частного ремонта: материалы и оборудование покупает заказчик по спецификациям проекта; монтаж ведёт подрядная бригада; приёмку скрытых работ ведёт автор проекта. Распределение закреплено по радиаторам, подоконникам, дверям, розеткам и выключателям, сантехническим приборам, светильникам и отделочным материалам. Схема уточняется договором подряда; состав подрядчиков и поставщиков остаётся вопросом К-12. | Утверждено: Кырлан А.С., автор проекта, 05.10.2026. Предложил: решение автора проекта, оформлено исполнителем по его поручению. |
| ИЗ-18 | 05.10.2026 | л. 3 — Список листов | Графы «Пров.» и «Н. контр.» основной надписи пусты (вопрос К-8); как с ними поступать — не записано. | Графы «Пров.» и «Н. контр.» остаются пустыми: независимой проверки и нормоконтроля проекта не было, автор проекта сам себе их не подписывает. Комплект выпускается предварительным: пока нет подписи проверяющего и нормоконтролёра, отличных от разработчика, он не считается окончательным. | Утверждено: Кырлан А.С., автор проекта, 05.10.2026. Предложил: решение автора проекта, оформлено исполнителем по его поручению. |
| ИЗ-19 | 05.10.2026 | л. 43 — План розеток и электровыводов полный альбом | Розетки ванной Р7 (стиральная машина) и Р8 (фен): по ПУЭ допустимы в зоне 3 через УЗО 30 мА, по британской норме BS 7671 (п. 701.512.3) — дальше 2,5 м от границы зоны 1; какая норма принята — вопрос К-6. | Принята норма ПУЭ (п. 7.1.48): розетки в зоне 3 помещения с ванной допустимы при защите УЗО 30 мА. Положение розеток не менялось. Основание: розетки вне зон 0–2 (до границы зоны 1: Р7 1630 мм, Р8 — 1441 мм), исполнение IP44, группы 14 и 15 защищены УЗО 30 мА типа А. Это сознательное отступление от зарубежной нормы BS 7671: в России она не действует, по ней в таком месте допустима только бритвенная розетка с разделительным трансформатором. Расстояние Р7 до угла (72 мм при норме от 150 мм) этим решением не затронуто — вопрос К-6. | Утверждено: Кырлан А.С., автор проекта, 05.10.2026. Предложил: решение автора проекта, оформлено исполнителем по его поручению. |
| ИЗ-20 | 30.10.2026 | л. 34 — План размещения дверей<br>л. 74 — Развёртки стен А, Б. Прихожая-коридор (пом. 7)<br>л. 16 — План размещения мебели и оборудования | Проём коридор → прихожая-коридор (стена В коридора, offset 500) выходил за общую стену: на развёртке стены А прихожей видны 770 из 900 мм. Шкаф-купе М_28 (1700) заканчивался в 60 мм от проёма двери детской 2. | Проём — offset 300 (целиком в общей стене, знак «*»: положение со скана, К-21). М_28 — 1600 мм, зазор до проёма 160 мм под наличник. Вход в гостиную — вопрос К-31 с заданием на обследование. | Не утверждено: подписи нет. решение исполнителя; предложение проектировщика, на утверждение А. С. Кырлана |

## Разделы, не сданные к выпуску (сводка ролей)


| № | Раздел | Состояние | Причина |
|---|---|---|---|
| 1 | Инженер слаботочки и умного дома | Не сдан | слаботочка входит в состав заказа (ИЗ-16); выпущен лист «План слаботочных сетей» (раздел электрика); отдельная ведомость слаботочки — кабельный журнал, состав слаботочного щита — не выпущена |

## Примечания


1. Номера листов — по ведомости рабочих чертежей комплекта (лист «Общие данные»).
2. Графа «Если решения нет» показывает состояние решения на листах; влияние на сроки и стоимость по пунктам не оценивалось.
3. Пункт, по которому принято решение, при следующем выпуске комплекта из таблиц исключается.

| | | | | | | | |
|---|---|---|---|---|---|---|---|
| | | | | | Проект: Четырёхкомнатная квартира | | |
| | Лист | № док. | Подпись | Дата | Открытые вопросы, принятые допущения и конфликты. Лист 5 из 5 | Стадия | Лист | Листов |
| Дизайнер | Кырлан А.С. | | | 04.11.26 | | П | 96 | 120 |


## Общий вид

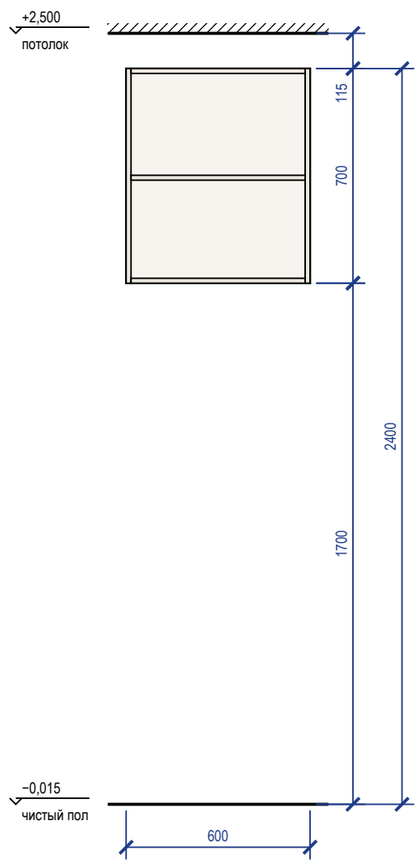


## Наполнение, размеры в свету

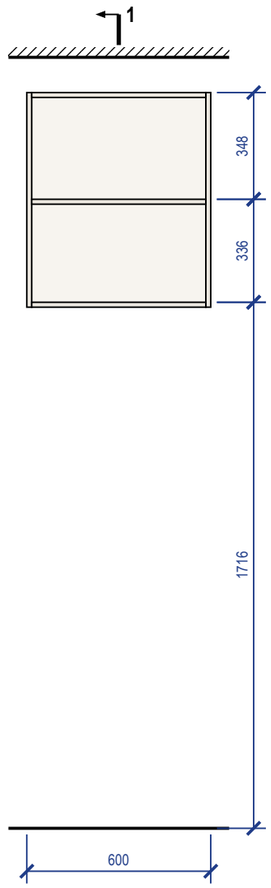



## Разрез 1-1

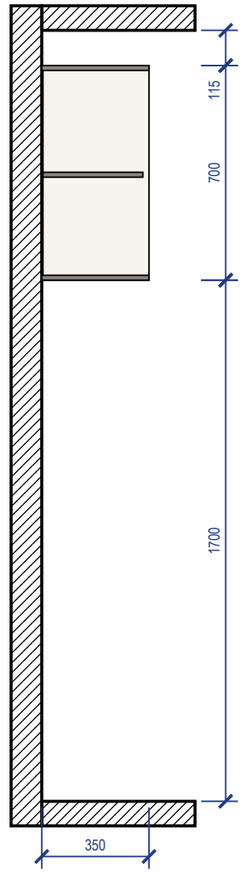


### Примечания


1. Размеры — в мм по чистовой отделке; изделие 600×350×700 (Ш×Г×В). Перед раскроем — контрольный замер цеха после чистовой отделки стен, пола и потолка.
2. Корпус — ЛДСП 16 мм, задняя стенка ХДФ 4 мм в паз, навесной корпус без цоколя, низ на 1700 мм от чистого пола; открытая система: без фасадов.
3. Кромка: скрытые торцы 0,4 мм, видимые 2 мм (ПВХ/АБС).
4. Присадка по 32-й системе — выполняет цех.
5. Зазор до потолка 115 мм — закрыть планкой в цвет корпуса при монтаже.
6. Навесной корпус — на стене: крепление к стене, 2 точки; основание стены и шаг анкеров — монтажная схема шкафов.

## 3D орто

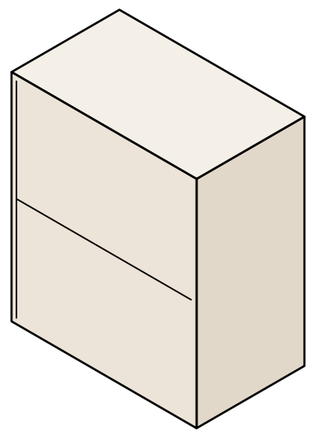


| | | | | | | |
|---|---|---|---|---|---|---|
| | | | | | Проект: Четырёхкомнатная квартира | **М 1:20** |
| | Лист | № док. | Подпись | Дата | | |
| Дизайнер | Кырлан А.С. | | | 04.11.26 | Система хранения М_07 | Стадия: П; Лист: Д_1; Листов: 120 |


## Общий вид

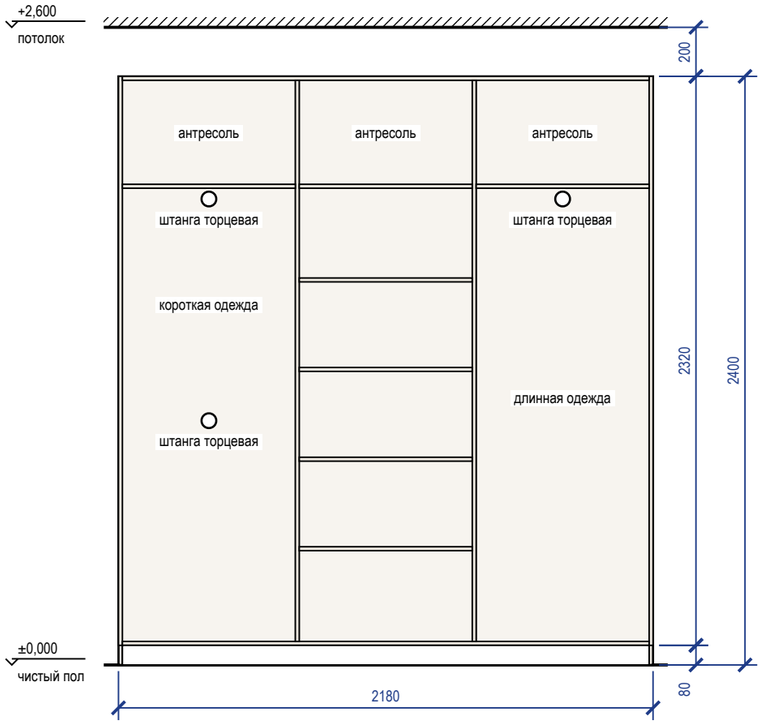



## Наполнение, размеры в свету

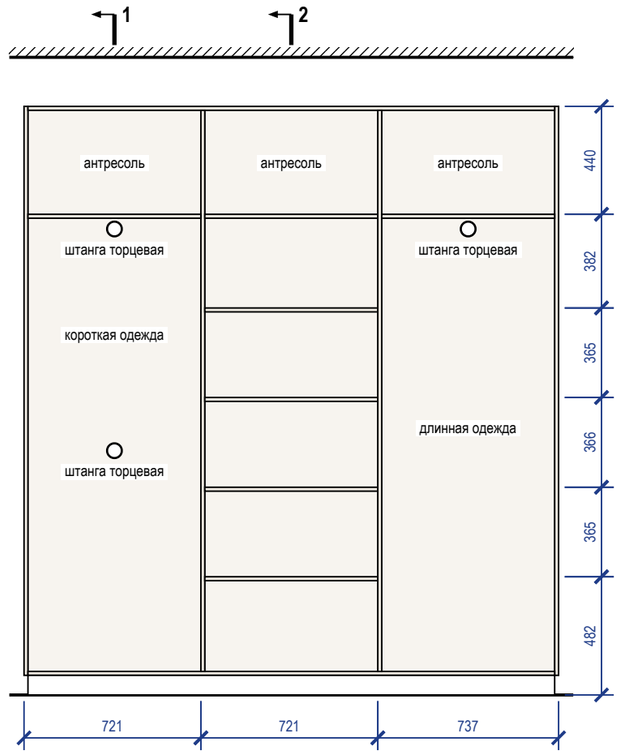


## Разрез 1-1

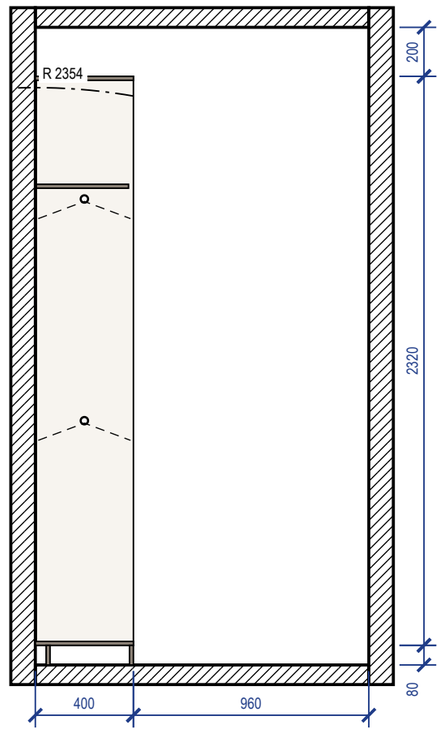



## Разрез 2-2

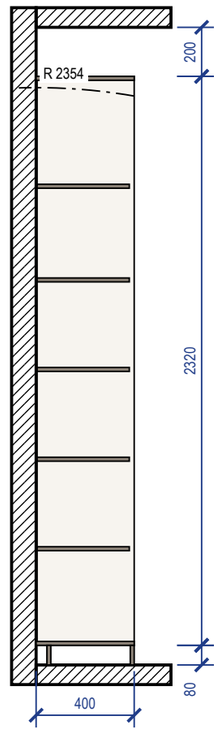


### Примечания


1. Размеры — в мм по чистовой отделке; изделие 2180×400×2400 (Ш×Г×В). Перед раскроем — контрольный замер цеха после чистовой отделки стен, пола и потолка.
2. Корпус — ЛДСП 16 мм, задняя стенка ХДФ 4 мм в паз, цоколь 80 мм на регулируемых опорах; открытая система: без фасадов.
3. Кромка: скрытые торцы 0,4 мм, видимые 2 мм (ПВХ/АБС).
4. Присадка по 32-й системе — выполняет цех.
5. Зазор до потолка 200 мм.
6. Подъём корпуса: диагональ боковины без цоколя $\sqrt{(2320^2 + 400^2)} = 2354$ мм < 2600 мм до потолка — корпус собирается лёжа, поднимается поворотом и ставится на цоколь.
7. Крепление к стене от опрокидывания: крепление к стене, 4 точки; основание стены и шаг анкеров — монтажная схема шкафов.
8. Проход перед изделием 960 мм показан на разрезе 1-1.

## 3D орто

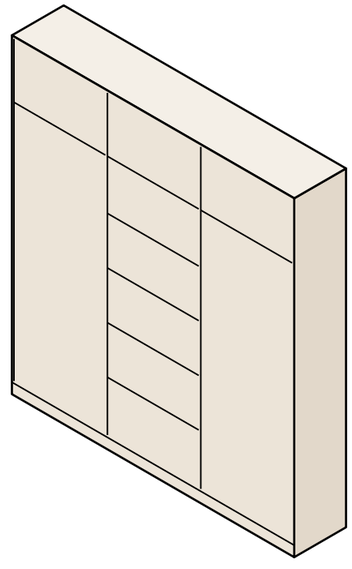

| | | | | | | |
|---|---|---|---|---|---|---|
| | | | | | Проект: Четырёхкомнатная квартира | **М 1:25** |
| | Лист | № док. | Подпись | Дата | | |
| Дизайнер | Кырлан А.С. | | | 04.11.26 | Система хранения М_08 | Стадия: П; Лист: Д_2; Листов: 120 |


## Общий вид

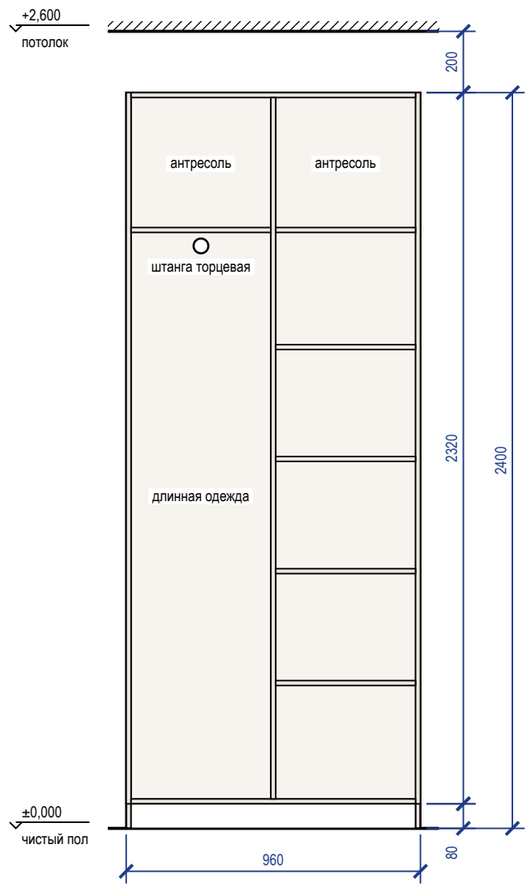



## Наполнение, размеры в свету




## Разрез 1-1

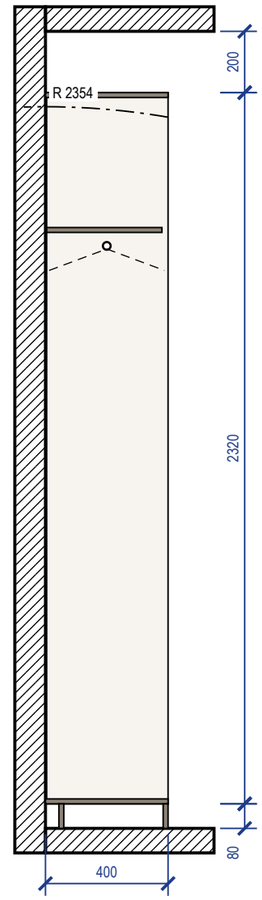



## Разрез 2-2

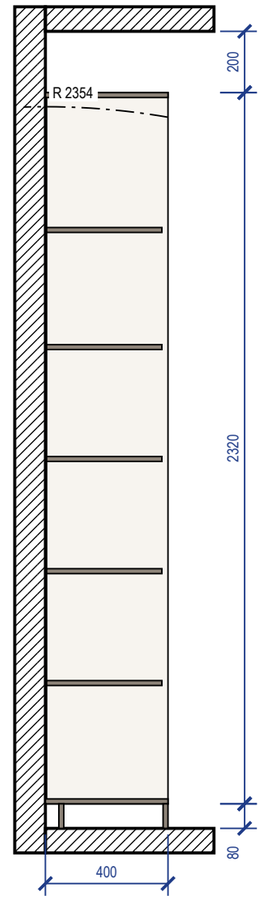


### Примечания


1. Размеры — в мм по чистовой отделке; изделие 960×400×2400 (Ш×Г×В). Перед раскроем — контрольный замер цеха после чистовой отделки стен, пола и потолка.
2. Корпус — ЛДСП 16 мм, задняя стенка ХДФ 4 мм в паз, цоколь 80 мм на регулируемых опорах; открытая система: без фасадов.
3. Кромка: скрытые торцы 0,4 мм, видимые 2 мм (ПВХ/АБС).
4. Присадка по 32-й системе — выполняет цех.
5. Зазор до потолка 200 мм.
6. Подъём корпуса: диагональ боковины без цоколя $\sqrt{(2320^2 + 400^2)} = 2354$ мм < 2600 мм до потолка — корпус собирается лёжа, поднимается поворотом и ставится на цоколь.
7. Крепление к стене от опрокидывания: крепление к стене, 3 точки; основание стены и шаг анкеров — монтажная схема шкафов.

## 3D орто

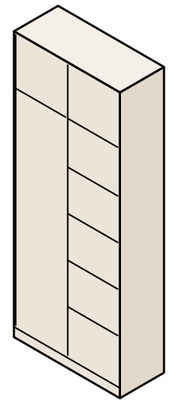


| | | | | | | |
|---|---|---|---|---|---|---|
| | | | | | Проект: Четырёхкомнатная квартира | **М 1:20** |
| | Лист | № док. | Подпись | Дата | | |
| Дизайнер | Кырлан А.С. | | | 04.11.26 | Система хранения М_09 | Стадия: П; Лист: Д_3; Листов: 120 |


## Вид с фасадами

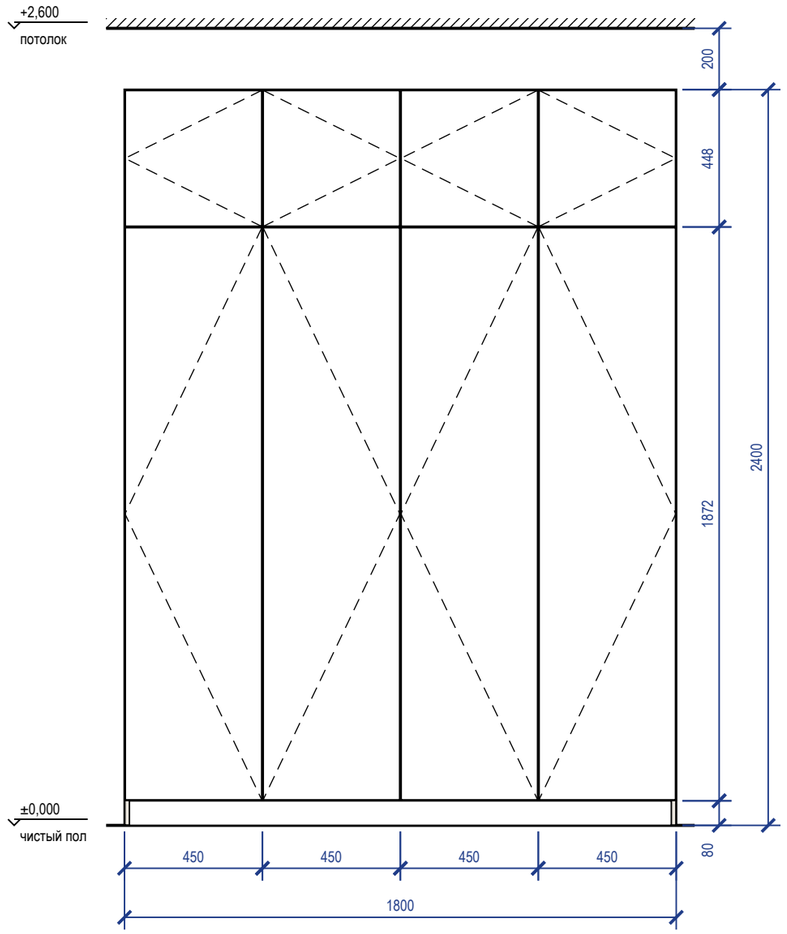



## Вид без фасадов

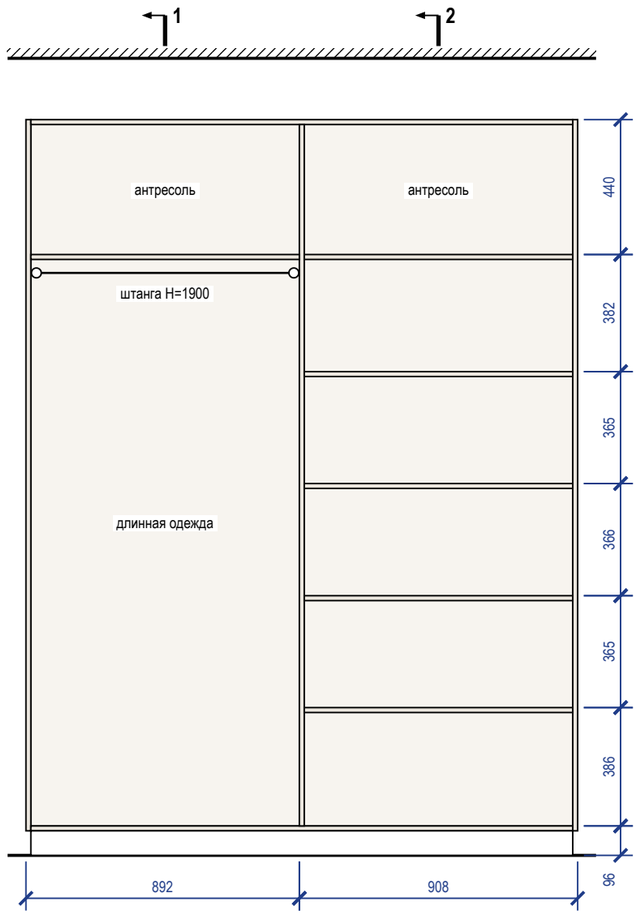


## Разрез 1-1

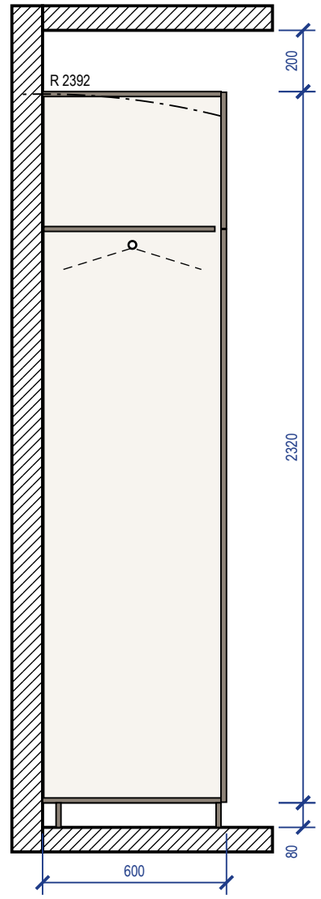



## Разрез 2-2

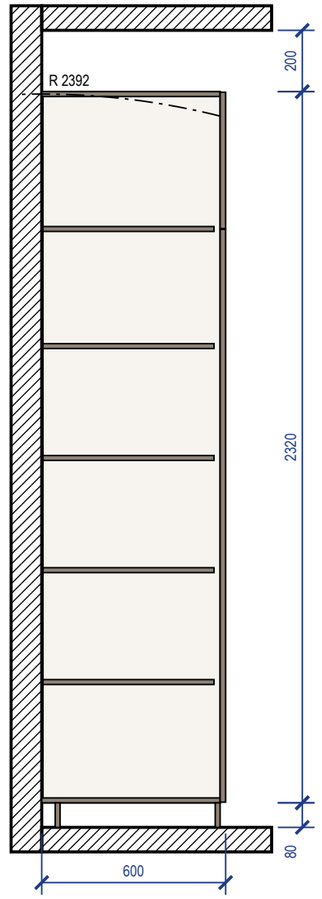


### Примечания


1. Размеры — в мм по чистовой отделке; изделие 1800×600×2400 (Ш×Г×В). Перед раскроем — контрольный замер цеха после чистовой отделки стен, пола и потолка.
2. Корпус — ЛДСП 16 мм, задняя стенка ХДФ 4 мм в паз, цоколь 80 мм на регулируемых опорах; фасады накладные — МДФ 18 мм, эмаль матовая, 18 мм; цвет — по колерной карте; петли с доводчиком: фасад 1869 мм — 4 петли, фасад 445 мм — 2 петли.
3. Кромка: скрытые торцы 0,4 мм, видимые 2 мм (ПВХ/АБС).
4. Номинальные зазоры: между фасадами 3 мм, фасад — стена и фасад — потолок не менее 3 мм, фасад ящика — стойка 2 мм.
5. Присадка по 32-й системе — выполняет цех.
6. Зазор до потолка 200 мм.
7. Подъём корпуса: диагональ боковины без цоколя $\sqrt{(2320^2 + 582^2)} = 2392$ мм < 2600 мм до потолка — корпус собирается лёжа, поднимается поворотом и ставится на цоколь.
8. Крепление к стене от опрокидывания: уголок к стене, 3 шт.; основание стены и шаг анкеров — монтажная схема шкафов.

## 3D орто

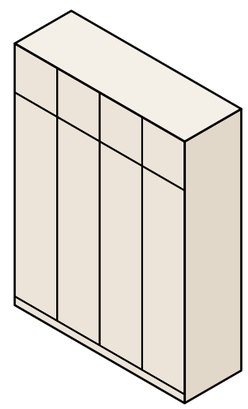


| | | | | | | |
|---|---|---|---|---|---|---|
| | | | | | Проект: Четырёхкомнатная квартира | **М 1:20** |
| | Лист | № док. | Подпись | Дата | | |
| Дизайнер | Кырлан А.С. | | | 04.11.26 | Шкаф распашной М_15 | Стадия: П; Лист: Д_4; Листов: 120 |


## Общий вид

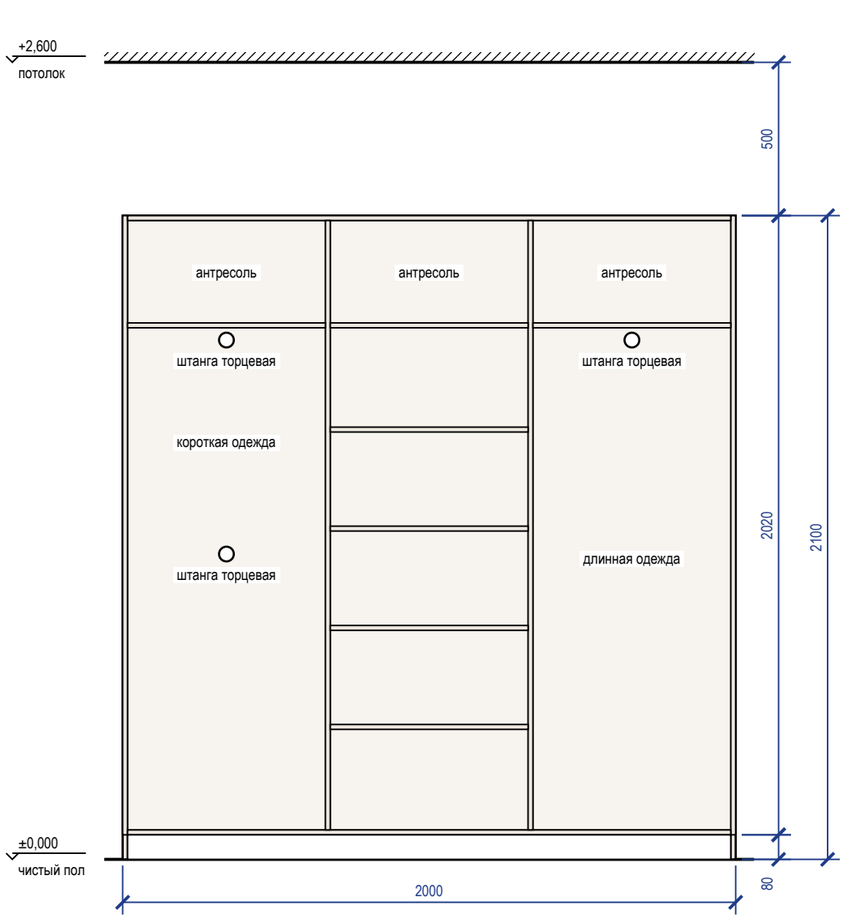



## Наполнение, размеры в свету

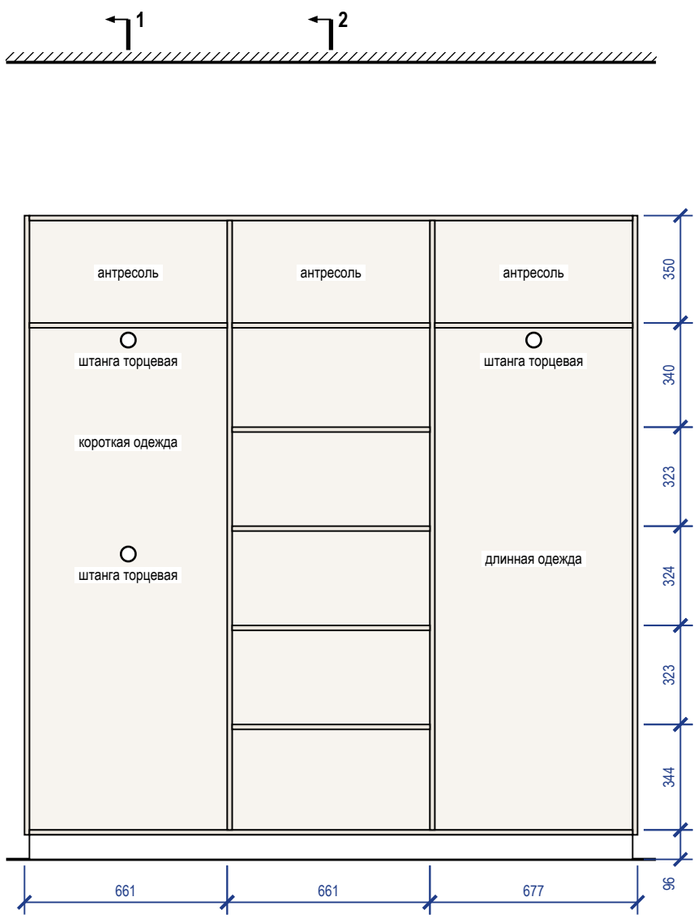


## Разрез 1-1

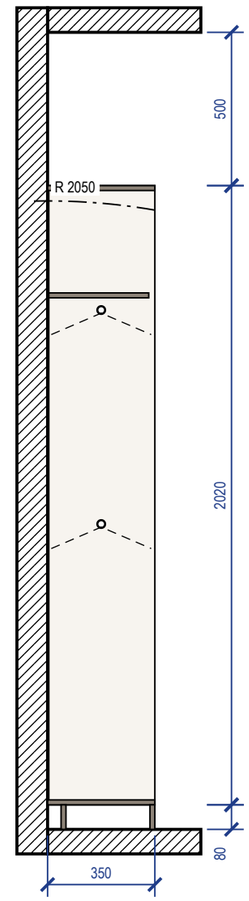



## Разрез 2-2

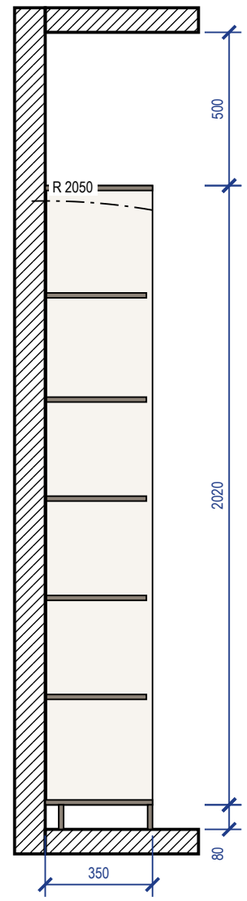


### Примечания


1. Размеры — в мм по чистовой отделке; изделие 2000×350×2100 (Ш×Г×В). Перед раскроем — контрольный замер цеха после чистовой отделки стен, пола и потолка.
2. Корпус — ЛДСП 16 мм, задняя стенка ХДФ 4 мм в паз, цоколь 80 мм на регулируемых опорах; открытая система: без фасадов.
3. Кромка: скрытые торцы 0,4 мм, видимые 2 мм (ПВХ/АБС).
4. Присадка по 32-й системе — выполняет цех.
5. Зазор до потолка 500 мм.
6. Подъём корпуса: диагональ боковины без цоколя $\sqrt{(2020^2 + 350^2)} = 2050$ мм < 2600 мм до потолка — корпус собирается лёжа, поднимается поворотом и ставится на цоколь.
7. Крепление к стене от опрокидывания: крепление к стене, 3 точки; основание стены и шаг анкеров — монтажная схема шкафов.

## 3D орто

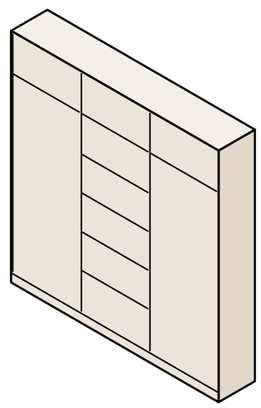


| | | | | | | |
|---|---|---|---|---|---|---|
| | | | | | Проект: Четырёхкомнатная квартира | **М 1:20** |
| | Лист | № док. | Подпись | Дата | | |
| Дизайнер | Кырлан А.С. | | | 04.11.26 | Система хранения М_17 | Стадия / Лист / Листов |
| | | | | | | П / Д_5 / 120 |


## Вид с фасадами

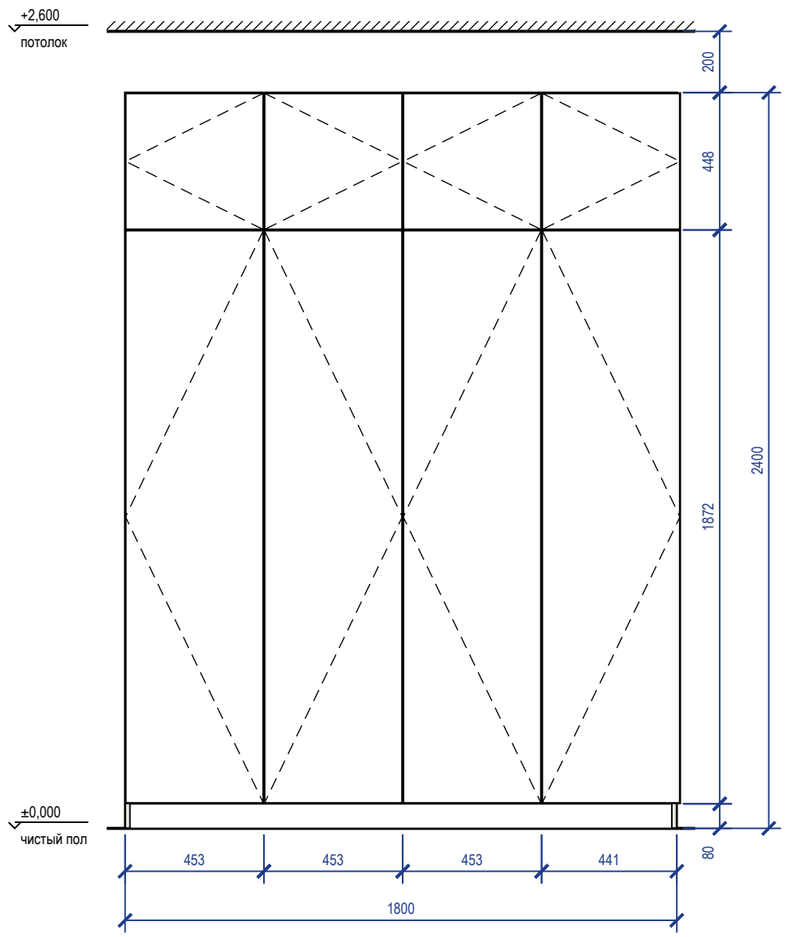


## Вид без фасадов

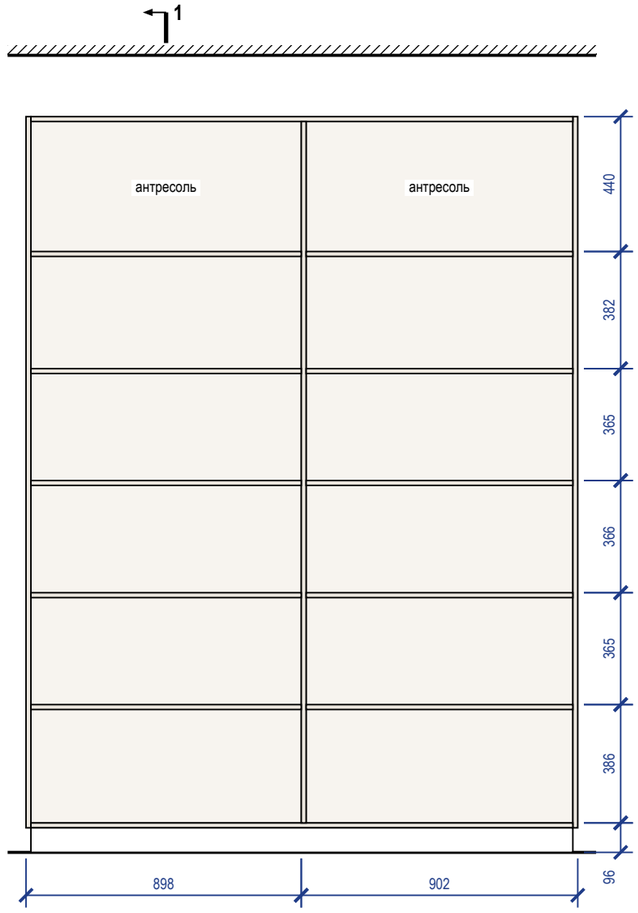



## Разрез 1-1

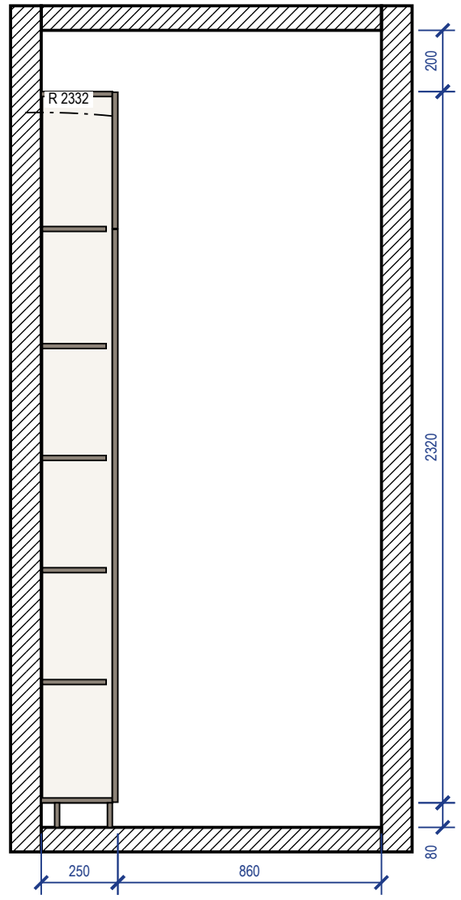


### Примечания


1. Размеры — в мм по чистовой отделке; изделие 1800×250×2400 (Ш×Г×В). Перед раскроем — контрольный замер цеха после чистовой отделки стен, пола и потолка.
2. Корпус — ЛДСП 16 мм, задняя стенка ХДФ 4 мм в паз, цоколь 80 мм на регулируемых опорах; фасады накладные — МДФ 18 мм, эмаль матовая, 18 мм; цвет — по колерной карте; петли с доводчиком: фасад 1869 мм — 4 петли, фасад 445 мм — 2 петли.
3. Кромка: скрытые торцы 0,4 мм, видимые 2 мм (ПВХ/АБС).
4. Номинальные зазоры: между фасадами 3 мм, фасад — стена и фасад — потолок не менее 3 мм, фасад ящика — стойка 2 мм.
5. Присадка по 32-й системе — выполняет цех.
6. Зазор до потолка 200 мм.
7. Подъём корпуса: диагональ боковины без цоколя √(2320² + 232²) = 2332 мм < 2600 мм до потолка — корпус собирается лёжа, поднимается поворотом и ставится на цоколь.
8. Крепление к стене от опрокидывания: крепление к стене, 4 точки; основание стены и шаг анкеров — монтажная схема шкафов.
9. Проход перед изделием 860 мм показан на разрезе 1-1.

## 3D орто

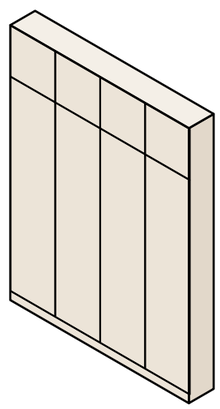


| | | | | | | |
|---|---|---|---|---|---|---|
| | | | | | Проект: Четырёхкомнатная квартира | **М 1:20** |
| | Лист | № док. | Подпись | Дата | | |
| Дизайнер | Кырлан А.С. | | | 04.11.26 | Система хранения М_18 | Стадия: П; Лист: Д_6; Листов: 120 |


## Вид с фасадами

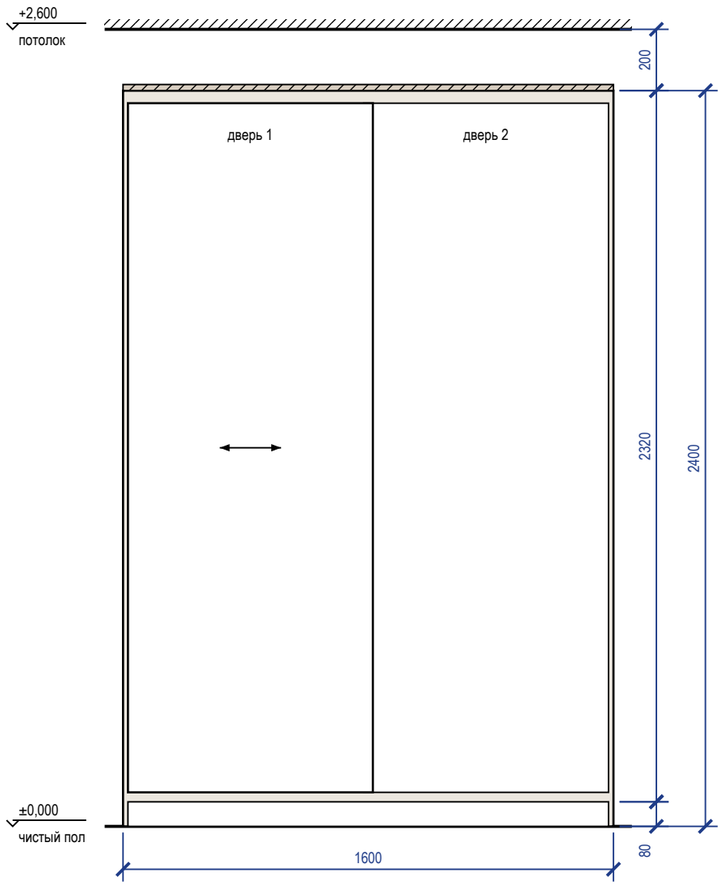



## Вид без фасадов

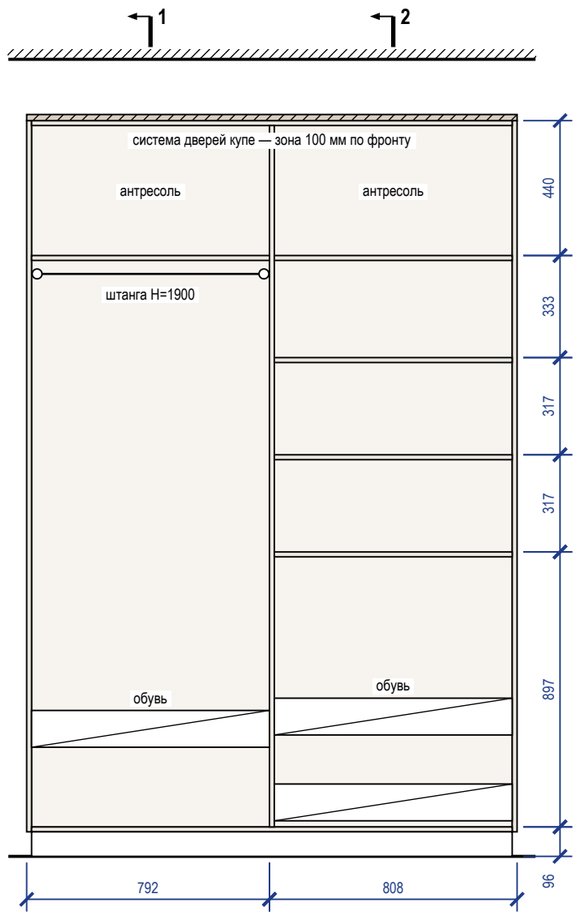


## Разрез 1-1

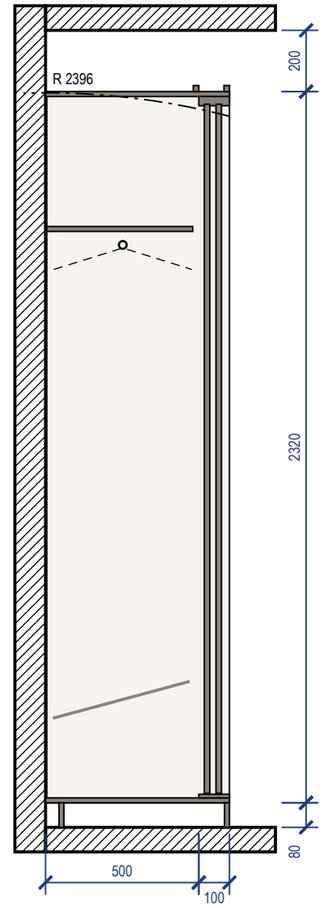



## Разрез 2-2

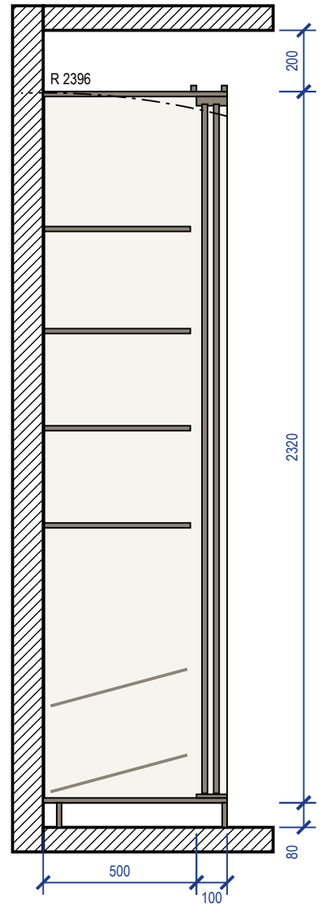


### Примечания


1. Размеры — в мм по чистовой отделке; изделие 1600×600×2400 (Ш×Г×В). Перед раскроем — контрольный замер цеха после чистовой отделки стен, пола и потолка.
2. Корпус — ЛДСП 16 мм, задняя стенка ХДФ 4 мм в паз, цоколь 80 мм на регулируемых опорах; двери купе — ЛДСП 10 мм в алюминиевом профиле; нахлёст 30 мм, ширина двери 799 мм, высота — проём минус 40 мм; цвет — по колерной карте.
3. Кромка: скрытые торцы 0,4 мм, видимые 2 мм (ПВХ/АБС).
4. Номинальные зазоры: дверь купе — боковина 3 мм, фасад ящика — стойка 2 мм; ящики внутри купе — с накладкой 30 мм на стойке со стороны нахлёста дверей.
5. Присадка по 32-й системе — выполняет цех.
6. Компенсатор 20 мм — короб из ЛДСП по фронту и торцам, подгоняется к потолку при монтаже (припуск 20 мм), крепится к корпусу и к потолку.
7. Подъём корпуса: диагональ боковины без цоколя $\sqrt{(2320^2 + 600^2)} = 2396$ мм < 2600 мм до потолка — корпус собирается лёжа, поднимается поворотом и ставится на цоколь.
8. Крепление к стене от опрокидывания: крепление к стене, 3 точки; основание стены и шаг анкеров — монтажная схема шкафов.

## 3D орто

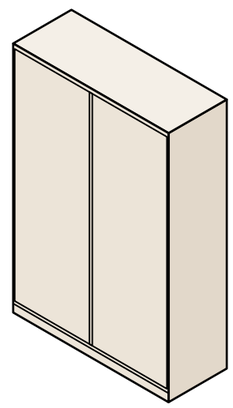


| | | | | | | |
|---|---|---|---|---|---|---|
| | | | | | Проект: Четырёхкомнатная квартира | **М 1:20** |
| | Лист | № док. | Подпись | Дата | | |
| Дизайнер | Кырлан А.С. | | | 04.11.26 | Шкаф-купе М_28 | Стадия: П; Лист: Д_7; Листов: 120 |


## Общий вид

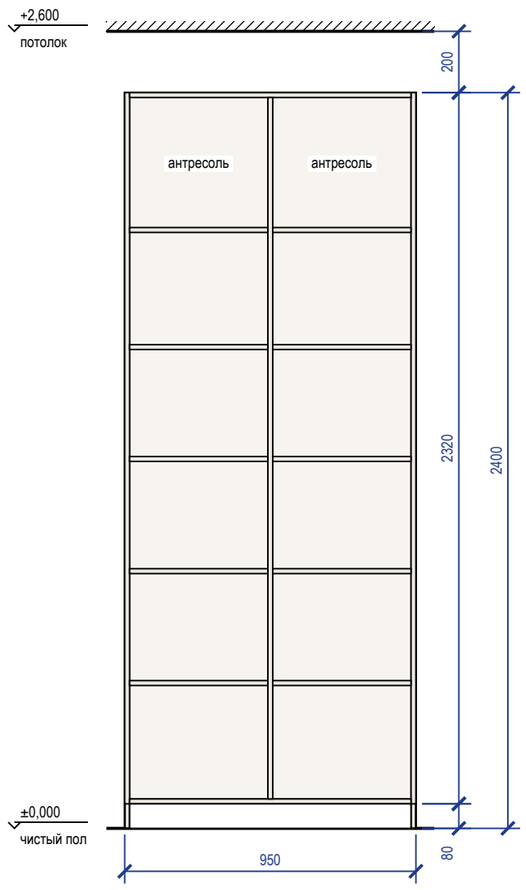


## Наполнение, размеры в свету

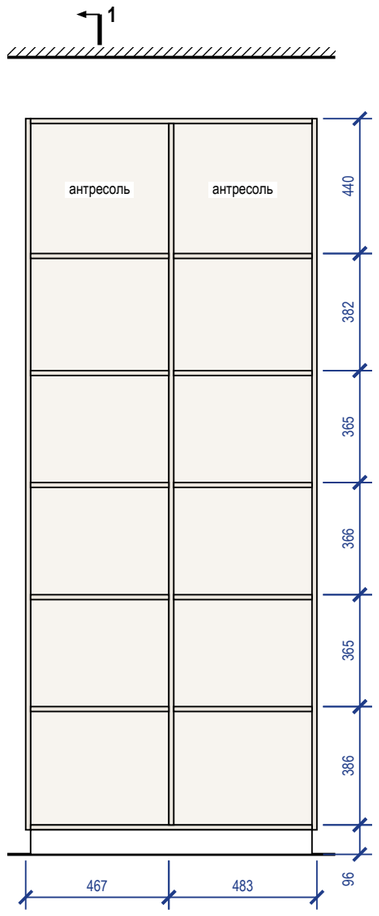



## Разрез 1-1

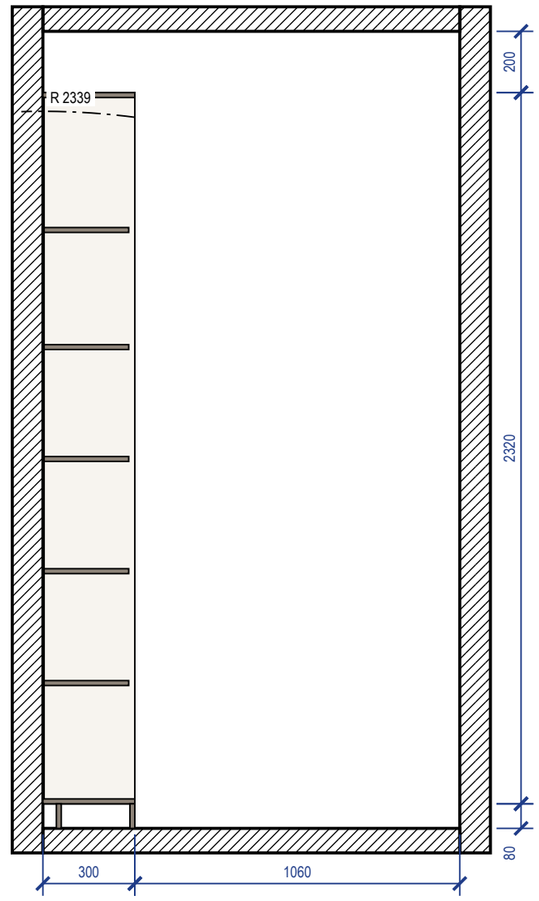


### Примечания


1. Размеры — в мм по чистовой отделке; изделие 950×300×2400 (Ш×Г×В). Перед раскроем — контрольный замер цеха после чистовой отделки стен, пола и потолка.
2. Корпус — ЛДСП 16 мм, задняя стенка ХДФ 4 мм в паз, цоколь 80 мм на регулируемых опорах; открытая система: без фасадов.
3. Кромка: скрытые торцы 0,4 мм, видимые 2 мм (ПВХ/АБС).
4. Присадка по 32-й системе — выполняет цех.
5. Зазор до потолка 200 мм.
6. Подъём корпуса: диагональ боковины без цоколя $\sqrt{(2320^2 + 300^2)} = 2339$ мм < 2600 мм до потолка — корпус собирается лёжа, поднимается поворотом и ставится на цоколь.
7. Крепление к стене от опрокидывания: крепление к стене, 3 точки; основание стены и шаг анкеров — монтажная схема шкафов.
8. Проход перед изделием 1060 мм показан на разрезе 1-1.

## 3D орто

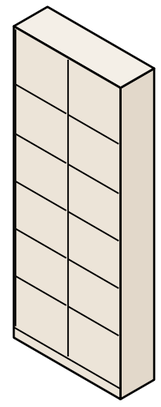


| | | | | | | |
|---|---|---|---|---|---|---|
| | | | | | Проект: Четырёхкомнатная квартира | **М 1:20** |
| | Лист | № док. | Подпись | Дата | | |
| Дизайнер | Кырлан А.С. | | | 04.11.26 | Система хранения М_31 | Стадия: П; Лист: Д_8; Листов: 120 |


## Общий вид

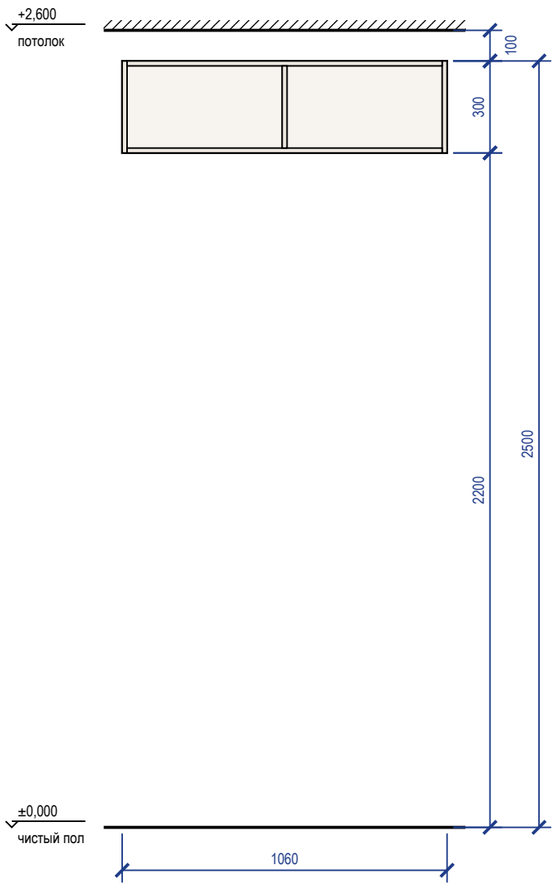


## Наполнение, размеры в свету

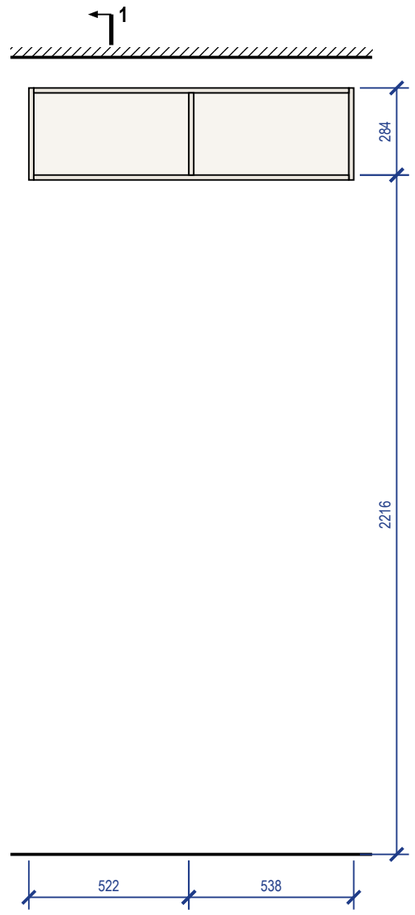



## Разрез 1-1

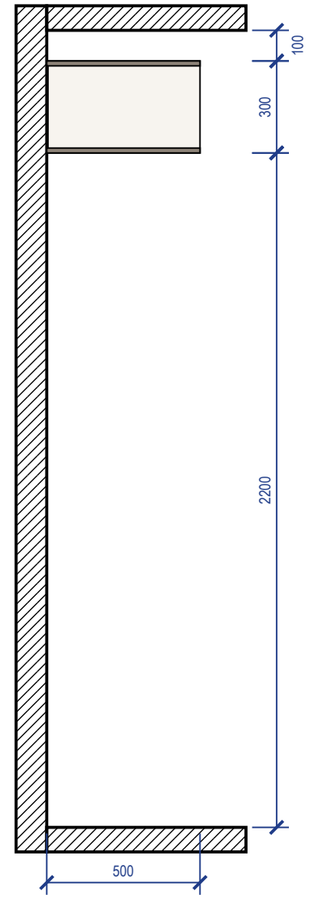


### Примечания


1. Размеры — в мм по чистовой отделке; изделие 1060×500×300 (Ш×Г×В). Перед раскроем — контрольный замер цеха после чистовой отделки стен, пола и потолка.
2. Корпус — ЛДСП 16 мм, задняя стенка ХДФ 4 мм в паз, навесной корпус без цоколя, низ на 2200 мм от чистого пола; открытая система: без фасадов.
3. Кромка: скрытые торцы 0,4 мм, видимые 2 мм (ПВХ/АБС).
4. Присадка по 32-й системе — выполняет цех.
5. Зазор до потолка 100 мм — закрыть планкой в цвет корпуса при монтаже.
6. Навесной корпус — на стене: крепление к стене, 4 точки; основание стены и шаг анкеров — монтажная схема шкафов.

## 3D орто

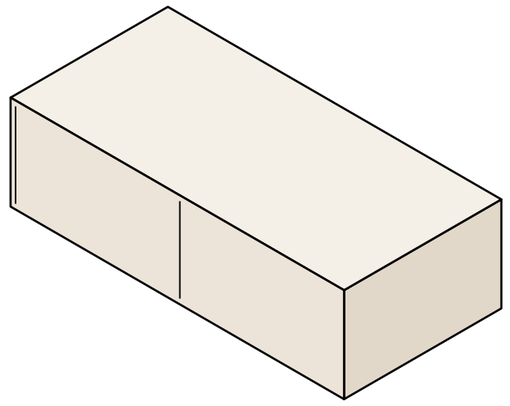


| | | | | | | | |
|---|---|---|---|---|---|---|---|
| | | | | | Проект: Четырёхкомнатная квартира | | М 1:20 |
| | Лист | № док. | Подпись | Дата | Система хранения M_32 | Стадия | Лист | Листов |
| Дизайнер | Кырлан А.С. | | | 04.11.26 | | П | Д_9 | 120 |


## Вид с фасадами

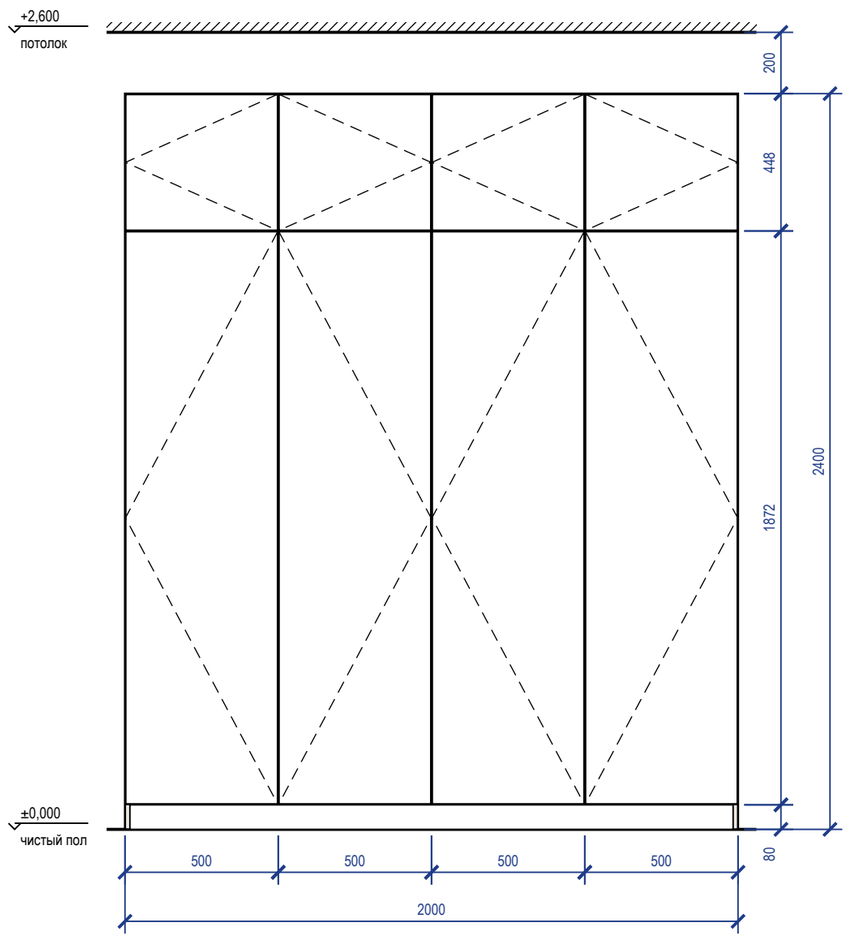



## Вид без фасадов

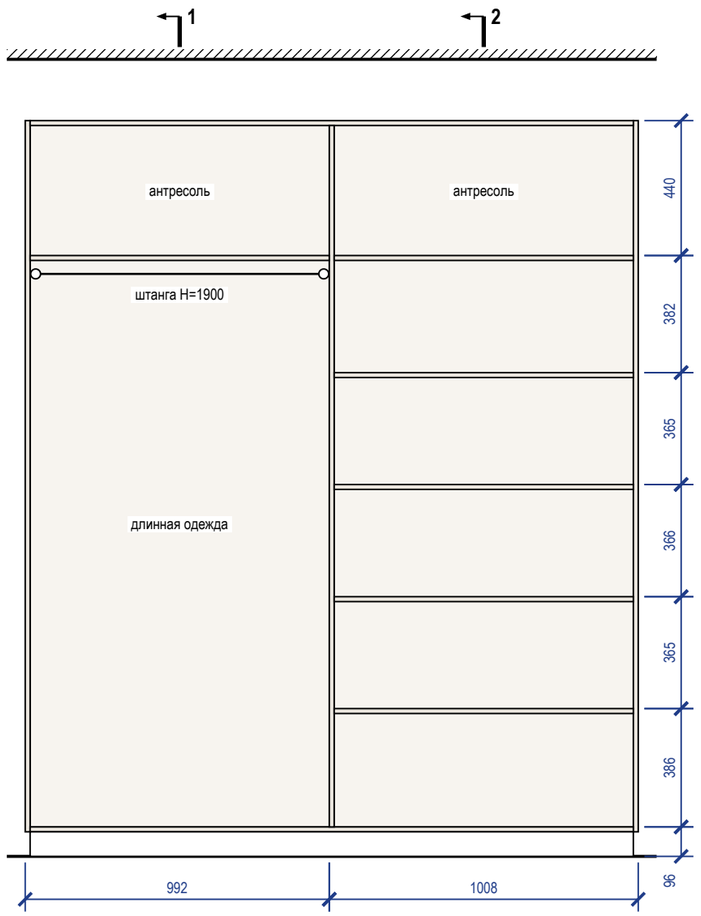


## Разрез 1-1

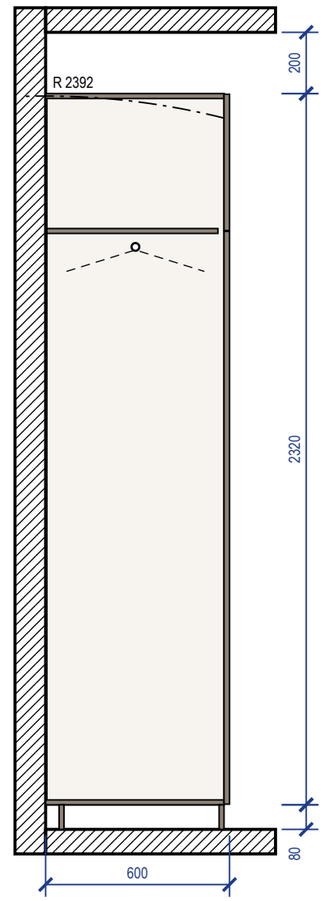



## Разрез 2-2

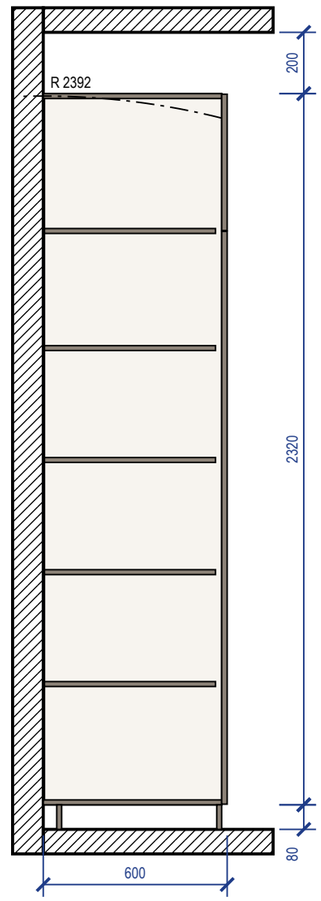


### Примечания


1. Размеры — в мм по чистовой отделке; изделие 2000×600×2400 (Ш×Г×В). Перед раскроем — контрольный замер цеха после чистовой отделки стен, пола и потолка.
2. Корпус — ЛДСП 16 мм, задняя стенка ХДФ 4 мм в паз, цоколь 80 мм на регулируемых опорах; фасады накладные — МДФ 18 мм, эмаль матовая, 18 мм; цвет — по колерной карте; петли с доводчиком: фасад 1869 мм — 4 петли, фасад 445 мм — 2 петли.
3. Кромка: скрытые торцы 0,4 мм, видимые 2 мм (ПВХ/АБС).
4. Номинальные зазоры: между фасадами 3 мм, фасад — стена и фасад — потолок не менее 3 мм, фасад ящика — стойка 2 мм.
5. Присадка по 32-й системе — выполняет цех.
6. Зазор до потолка 200 мм.
7. Подъём корпуса: диагональ боковины без цоколя $\sqrt{(2320^2 + 582^2)} = 2392$ мм < 2600 мм до потолка — корпус собирается лёжа, поднимается поворотом и ставится на цоколь.
8. Крепление к стене от опрокидывания: уголок к стене, 3 шт.; основание стены и шаг анкеров — монтажная схема шкафов.

## 3D орто

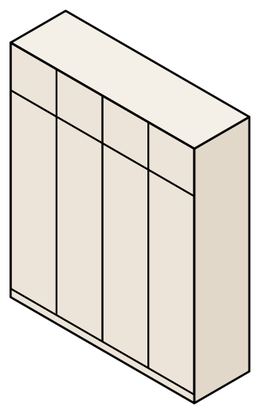


| | | | | | | |
|---|---|---|---|---|---|---|
| | | | | | Проект: Четырёхкомнатная квартира | **М 1:20** |
| | Лист | № док. | Подпись | Дата | | |
| Дизайнер | Кырлан А.С. | | | 04.11.26 | Шкаф распашной М_34 | Стадия: П; Лист: Д_10; Листов: 120 |


## Общий вид

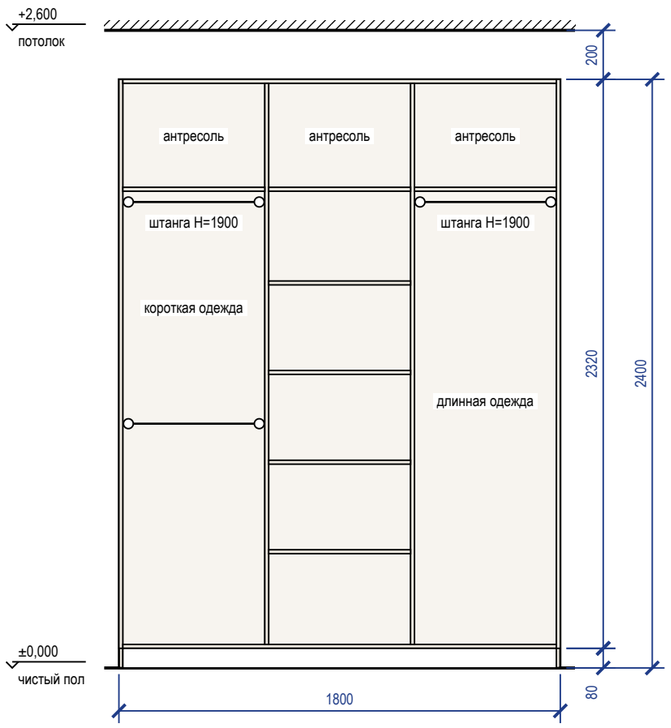



## Наполнение, размеры в свету

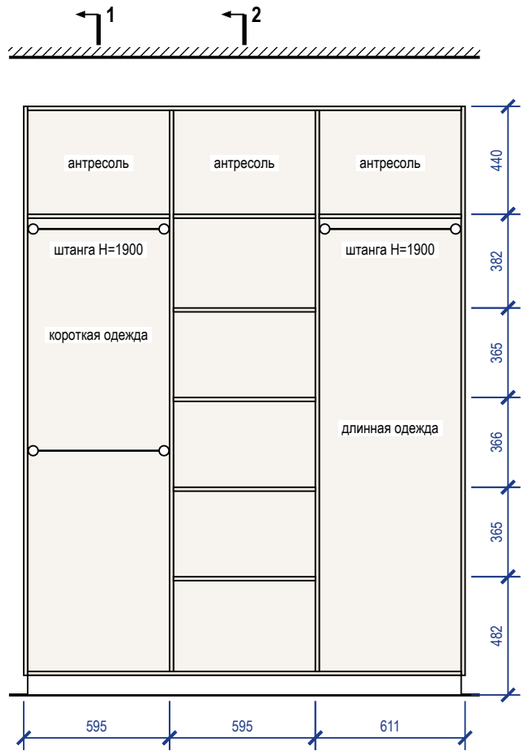


## Разрез 1-1

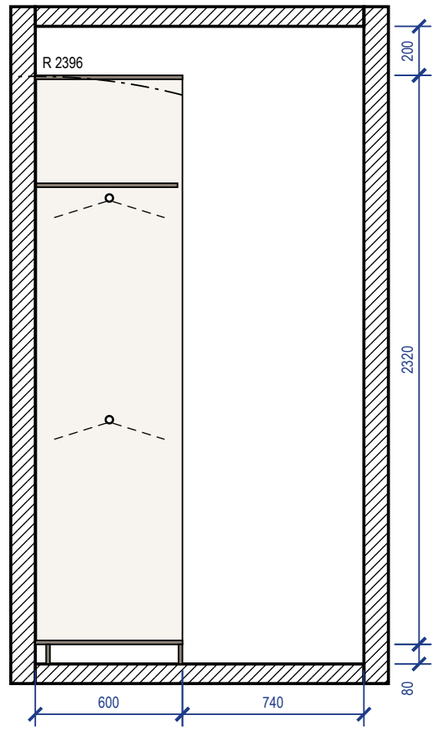



## Разрез 2-2

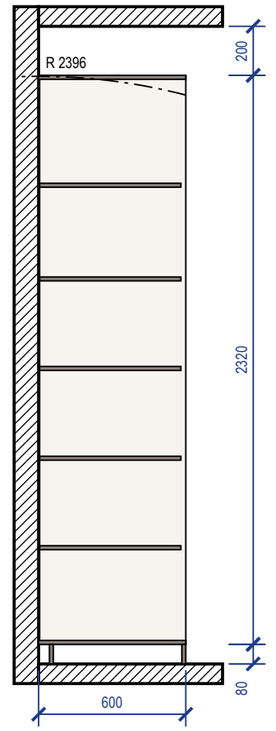


### Примечания


1. Размеры — в мм по чистовой отделке; изделие 1800×600×2400 (Ш×Г×В). Перед раскроем — контрольный замер цеха после чистовой отделки стен, пола и потолка.
2. Корпус — ЛДСП 16 мм, задняя стенка ХДФ 4 мм в паз, цоколь 80 мм на регулируемых опорах; открытая система: без фасадов.
3. Кромка: скрытые торцы 0,4 мм, видимые 2 мм (ПВХ/АБС).
4. Присадка по 32-й системе — выполняет цех.
5. Зазор до потолка 200 мм.
6. Подъём корпуса: диагональ боковины без цоколя $\sqrt{(2320^2 + 600^2)} = 2396$ мм < 2600 мм до потолка — корпус собирается лёжа, поднимается поворотом и ставится на цоколь.
7. Крепление к стене от опрокидывания: крепление к стене, 4 точки; основание стены и шаг анкеров — монтажная схема шкафов.
8. Проход перед изделием 740 мм показан на разрезе 1-1.

## 3D орто

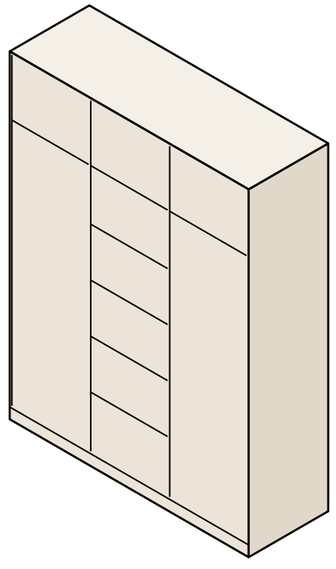


| | | | | | | |
|---|---|---|---|---|---|---|
| | | | | | Проект: Четырёхкомнатная квартира | **М 1:25** |
| | Лист | № док. | Подпись | Дата | | |
| Дизайнер | Кырлан А.С. | | | 04.11.26 | Система хранения М_38 | Стадия: П; Лист: Д_11; Листов: 120 |


## Общий вид

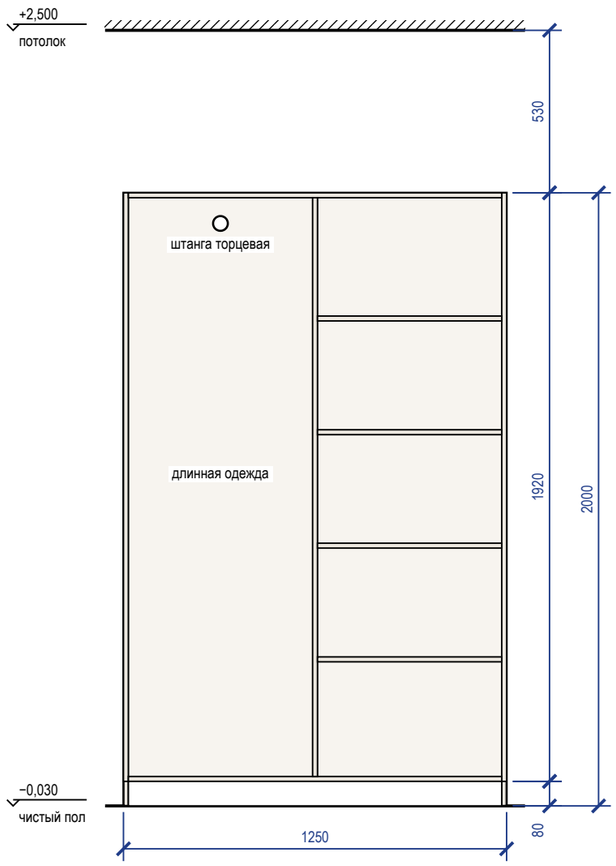



## Наполнение, размеры в свету

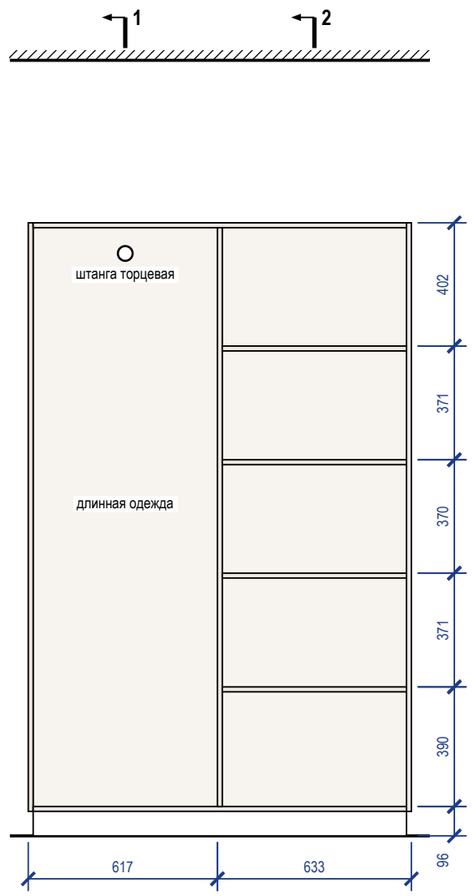


## Разрез 1-1

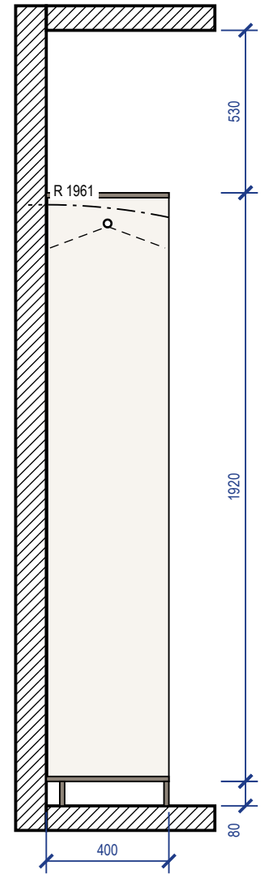



## Разрез 2-2

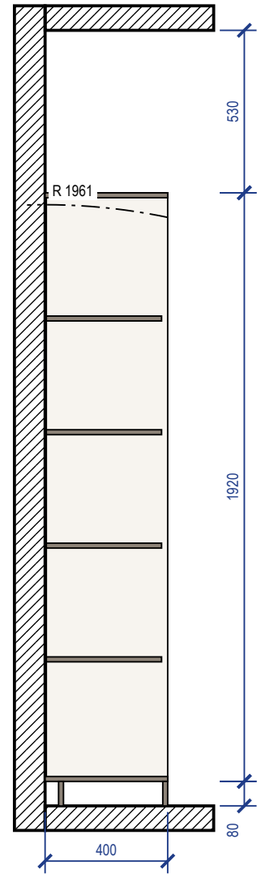


### Примечания


1. Размеры — в мм по чистовой отделке; изделие 1250×400×2000 (Ш×Г×В). Перед раскроем — контрольный замер цеха после чистовой отделки стен, пола и потолка.
2. Корпус — ЛДСП 16 мм, задняя стенка ХДФ 4 мм в паз, цоколь 80 мм на регулируемых опорах; открытая система: без фасадов.
3. Кромка: скрытые торцы 0,4 мм, видимые 2 мм (ПВХ/АБС).
4. Присадка по 32-й системе — выполняет цех.
5. Зазор до потолка 530 мм.
6. Подъём корпуса: диагональ боковины без цоколя $\sqrt{(1920^2 + 400^2)} = 1961$ мм < 2530 мм до потолка — корпус собирается лёжа, поднимается поворотом и ставится на цоколь.
7. Крепление к стене от опрокидывания: крепление к стене, 3 точки; основание стены и шаг анкеров — монтажная схема шкафов.

## 3D орто

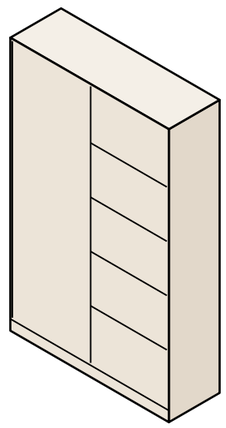


| | | | | | | |
|---|---|---|---|---|---|---|
| | | | | | Проект: Четырёхкомнатная квартира | **М 1:20** |
| | Лист | № док. | Подпись | Дата | | |
| Дизайнер | Кырлан А.С. | | | 04.11.26 | Система хранения М_39 | Стадия: П; Лист: Д_12; Листов: 120 |


## Общий вид

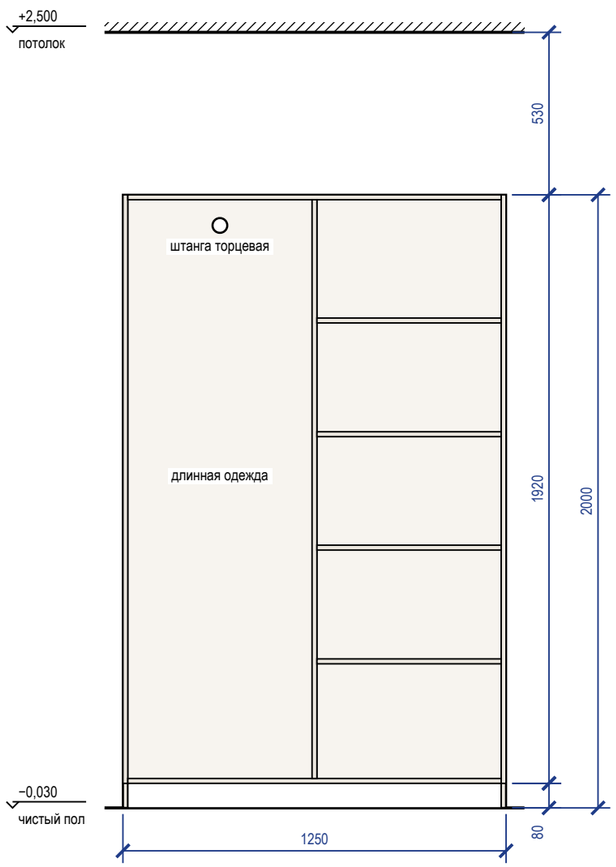



## Наполнение, размеры в свету

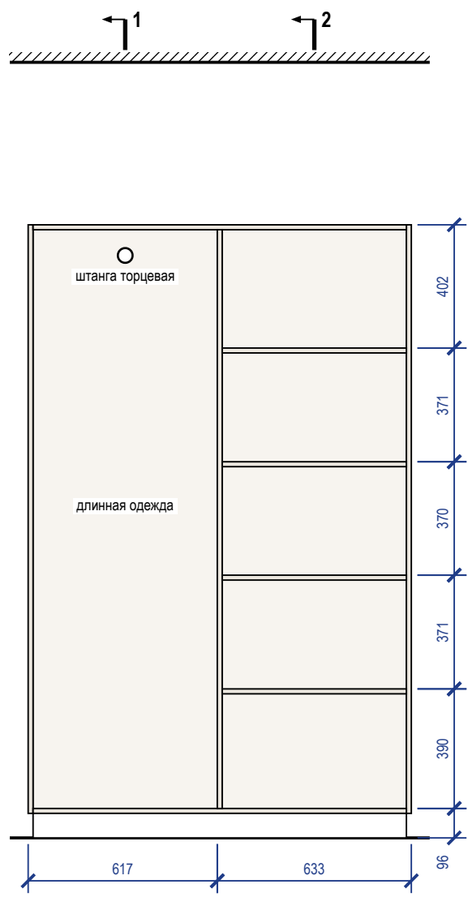


## Разрез 1-1

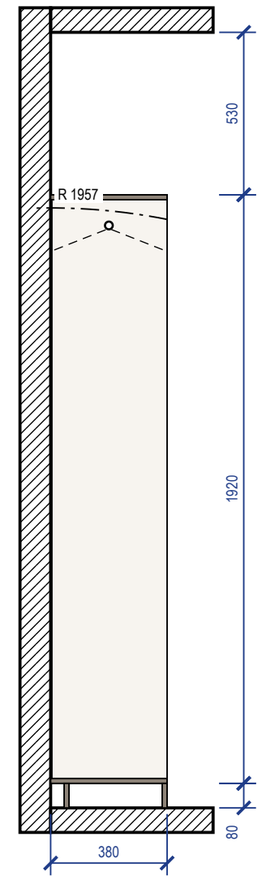



## Разрез 2-2

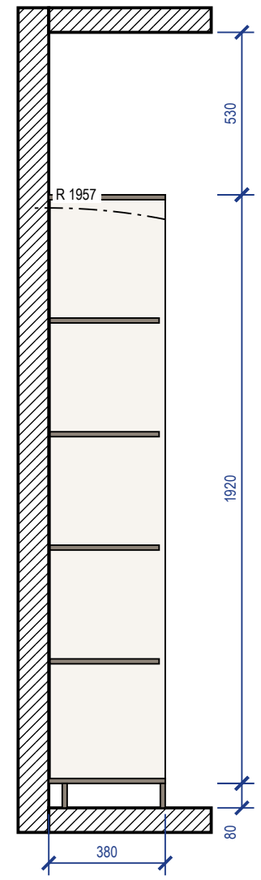


### Примечания


1. Размеры — в мм по чистовой отделке; изделие 1250×380×2000 (Ш×Г×В). Перед раскроем — контрольный замер цеха после чистовой отделки стен, пола и потолка.
2. Корпус — ЛДСП 16 мм, задняя стенка ХДФ 4 мм в паз, цоколь 80 мм на регулируемых опорах; открытая система: без фасадов.
3. Кромка: скрытые торцы 0,4 мм, видимые 2 мм (ПВХ/АБС).
4. Присадка по 32-й системе — выполняет цех.
5. Зазор до потолка 530 мм.
6. Подъём корпуса: диагональ боковины без цоколя $\sqrt{(1920^2 + 380^2)} = 1957$ мм < 2530 мм до потолка — корпус собирается лёжа, поднимается поворотом и ставится на цоколь.
7. Крепление к стене от опрокидывания: крепление к стене, 3 точки; основание стены и шаг анкеров — монтажная схема шкафов.

## 3D орто

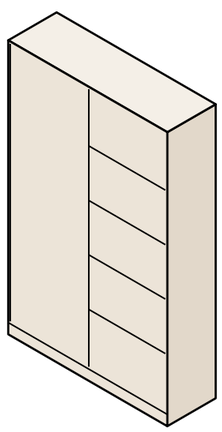


| | | | | | | |
|---|---|---|---|---|---|---|
| | | | | | Проект: Четырёхкомнатная квартира | **М 1:20** |
| | Лист | № док. | Подпись | Дата | | |
| Дизайнер | Кырлан А.С. | | | 04.11.26 | Система хранения М_40 | Стадия: П; Лист: Д_13; Листов: 120 |


## Вид с фасадами

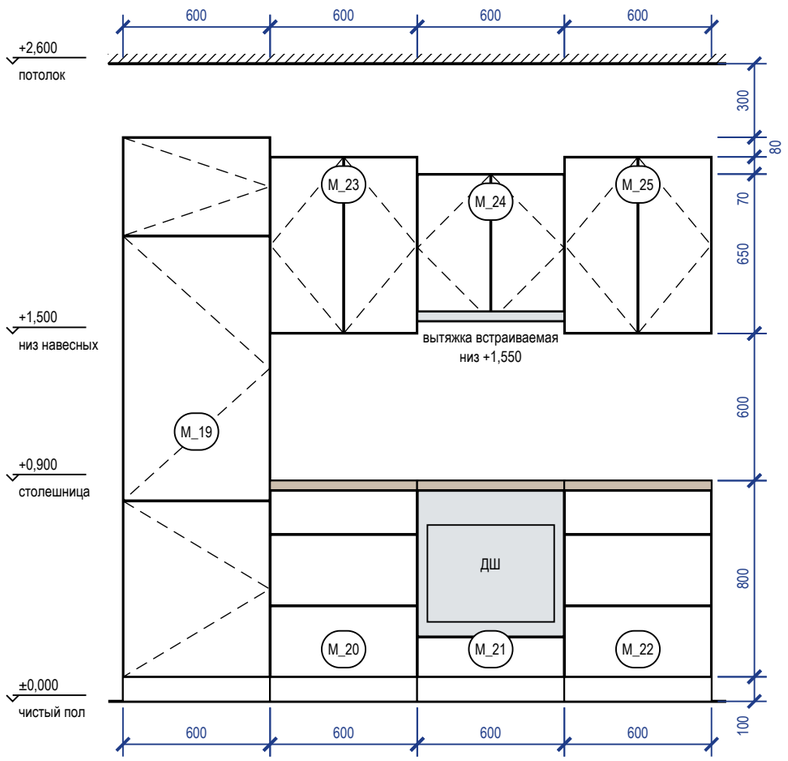



## Вид без фасадов (наполнение, выводы)

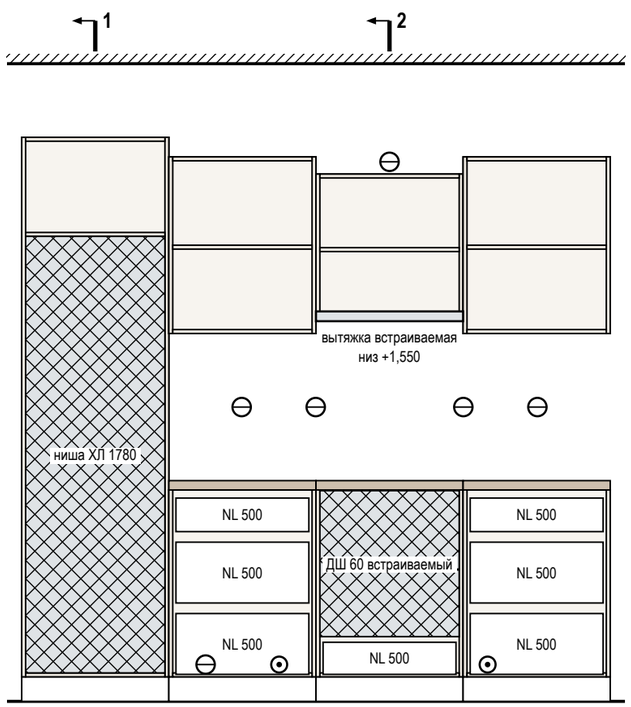



## Разрез 1-1

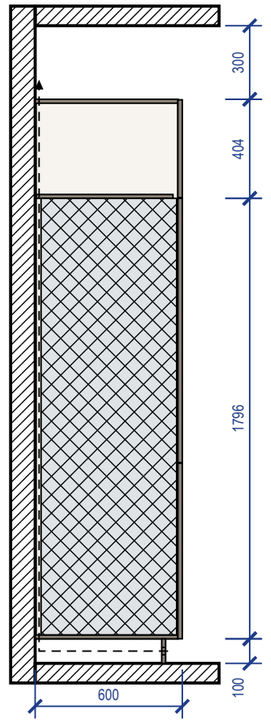


## Разрез 2-2

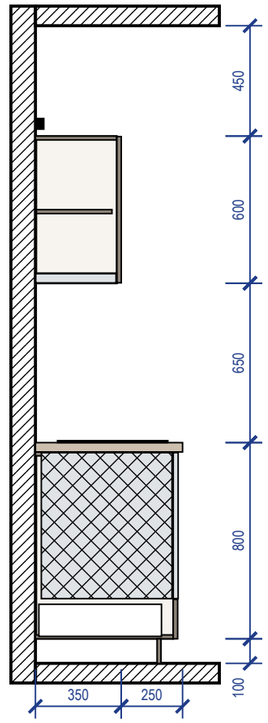


## 3D орто

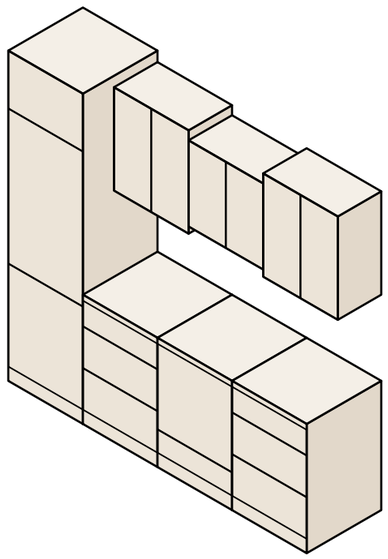


## Примечания


1. Размеры — в мм по чистовой отделке, вид из помещения; марки — как на плане расстановки. Перед раскроем — контрольный замер цеха после фартука и пола.
2. Корпуса — ЛДСП 16 мм, задняя стенка ХДФ 4 мм; фасады — МДФ, эмаль матовая 18 мм, цвет по колерной карте; столешница 38 мм, свес 20 мм; цоколь 100 мм.
3. Кромка: скрытые торцы 0,4 мм, видимые 2 мм. Номинальные зазоры: между фасадами 3 мм, фасад — столешница 3 мм, фасад — стена не менее 3 мм.
4. Ящики полного выдвижения и петли — с доводчиком; присадка по 32-й системе — выполняет цех.
5. Вытяжка встраивается в дно навесного модуля M_24 над варочной: её низ на 1550 мм от пола, 650 мм над панелью (не меньше 650 мм).
6. Ниши техники (холодильник — ориентир 1780 мм) — по монтажным схемам выбранных моделей: решётка в цоколе и канал за пеналом холодильника, зазор за духовым шкафом, фасад ПММ на двери машины.

| | | | | | | |
|---|---|---|---|---|---|---|
| | | | | | Проект: Четырёхкомнатная квартира | **М 1:25** |
| | Лист | № док. | Подпись | Дата | Кухня (пом. 6). Развёртка гарнитура | Стадия / Лист / Листов |
| Дизайнер | Кырлан А.С. | | | 04.11.26 | | П / Д_14 / 120 |


## Вид с фасадами

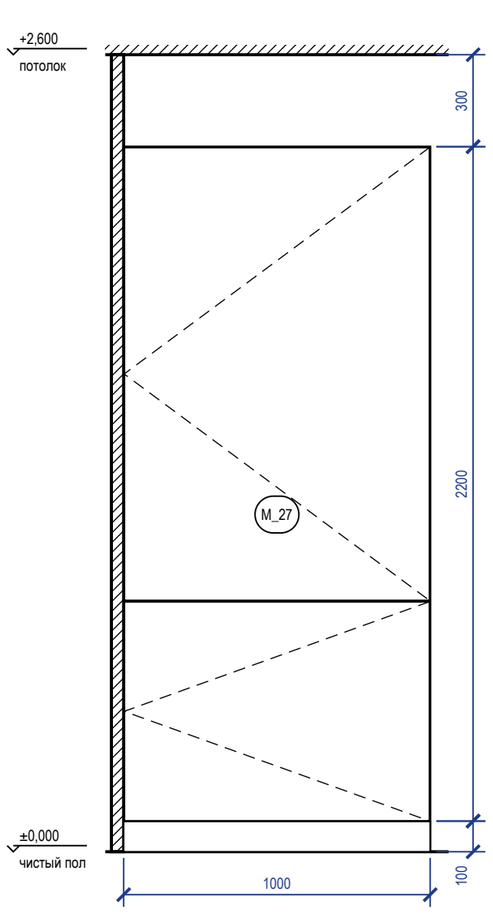



## Вид без фасадов (наполнение, выводы)

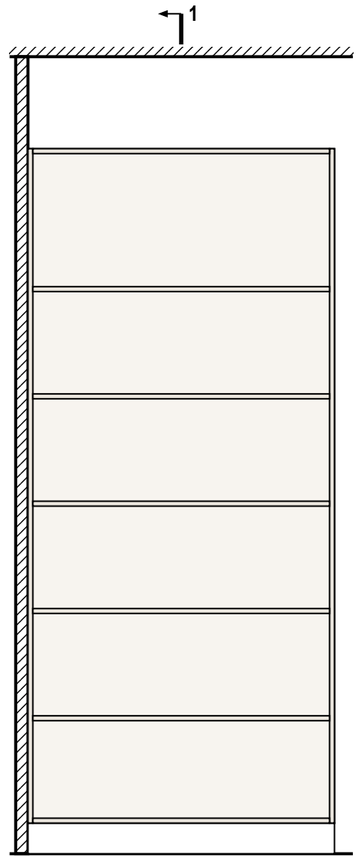


## Разрез 1-1

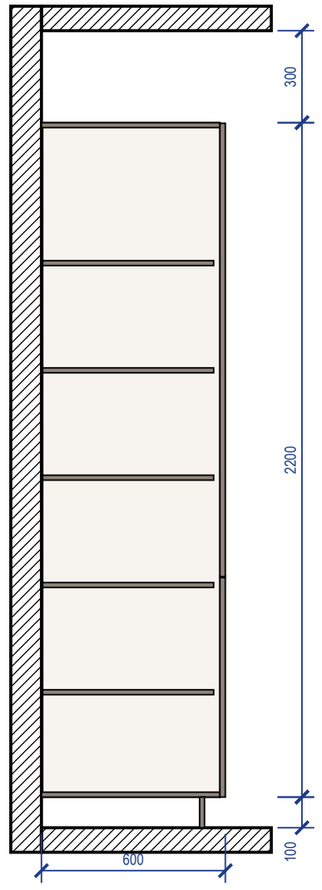


## 3D орто

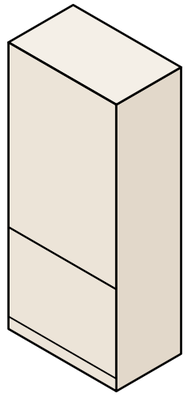


## Примечания

1. Размеры — в мм по чистовой отделке, вид из помещения; марки — как на плане расстановки. Перед раскроем — контрольный замер цеха после фартука и пола.
2. Корпуса — ЛДСП 16 мм, задняя стенка ХДФ 4 мм; фасады — МДФ, эмаль матовая 18 мм, цвет по колерной карте; столешница 38 мм, свес 20 мм; цоколь 100 мм.
3. Кромка: скрытые торцы 0,4 мм, видимые 2 мм. Номинальные зазоры: между фасадами 3 мм, фасад — столешница 3 мм, фасад — стена не менее 3 мм.
4. Ящики полного выдвижения и петли — с доводчиком; присадка по 32-й системе — выполняет цех.
5. Ниши техники — по монтажным схемам выбранных моделей: решётка в цоколе и канал за пеналом холодильника, зазор за духовым шкафом, фасад ПММ на двери машины.


| | | | | | | |
|---|---|---|---|---|---|---|
| | | | | | Проект: Четырёхкомнатная квартира | **М 1:20** |
| | Лист | № док. | Подпись | Дата | Кухня (пом. 6). Развёртка гарнитура | Стадия / Лист / Листов |
| Дизайнер | Кырлан А.С. | | | 04.11.26 | | П / Д_15 / 120 |

## План (вид сверху)

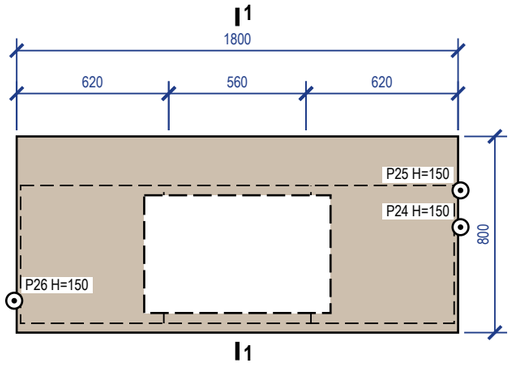



▲ рабочая сторона — северная (к стене А), проход 1200


## Вид с рабочей стороны

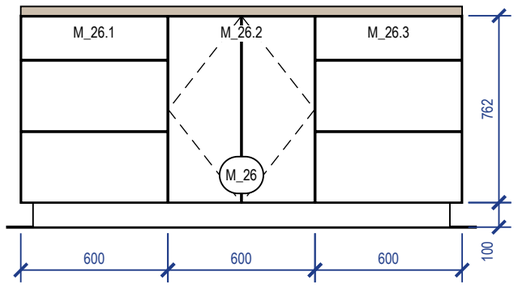



## Вид без фасадов (наполнение, вывод)

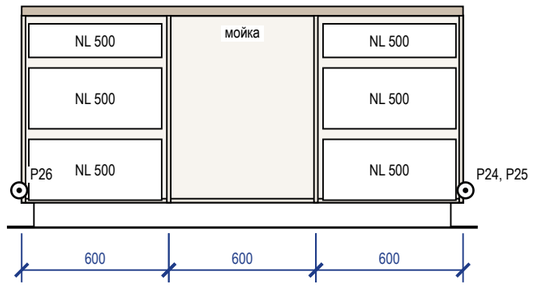


## Разрез 1-1

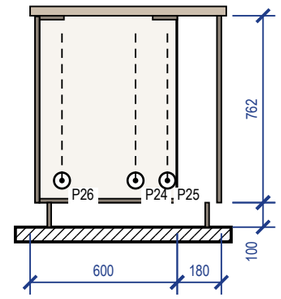


## 3D орто

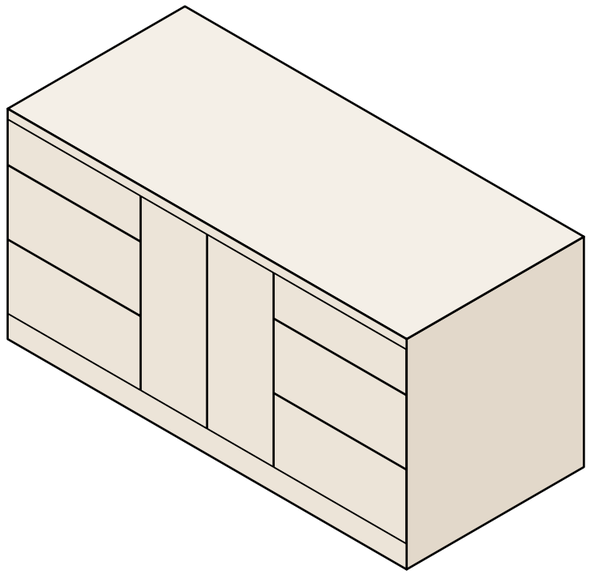

## Примечания

1. Размеры — в мм по чистовому полу; перед раскроем — контрольный замер цеха после укладки пола. Остров крепится к полу (уголки в цоколе), выравнивается опорами ±20 мм.
2. Корпуса — ЛДСП 16 мм, задняя стенка ХДФ 4 мм; фасады — МДФ, эмаль матовая 18 мм; столешница 38 мм, свес 20 мм по периметру; цоколь 100 мм с отступом 50 мм.
3. Кромка: скрытые торцы 0,4 мм, видимые 2 мм. Номинальные зазоры: между фасадами 3 мм, фасад — столешница 3 мм.
4. Рабочая сторона — северная (к стене А): проход 1200 мм; с тыла — глухая панель. Членение и сторона — предложение мебельщика.
5. Питание: P24 — торцевая панель острова M_26: мелкая техника, H=150; P25 — торцевая панель острова M_26: мелкая техника, H=150; P26 — посудомоечная машина в острове M_26, H=150; кабель — внутри модуля до панели, доступ через съёмный цоколь.

## Спецификация изделия M_26

| Поз. | Наименование | Тип, размер | Кол. |
|---|---|---|---|
| M_26.1 | модуль с ящиками | 600×800×900 | 1 |
| M_26.2 | модуль под мойку | 600×800×900 | 1 |
| M_26.3 | модуль с ящиками | 600×800×900 | 1 |
| M_26.2 | Мойка врезная / подстольная с сифоном | вырез по шаблону, ориентир 760 × 480 | 1 |
| | Направляющие полного выдвижения с доводчиком NL 500 | пара | 6 |
| | Ручка-профиль | латунь матовая | 8 |
| | Петля накладная 110° с доводчиком | чашка 35 мм | 4 |
| | Опора кухонная регулируемая 100–120 мм | + клипса цоколя | 12 |
| | Уголок крепления острова к полу | стальной, в цоколе | 4 |

| | | | | | | |
|---|---|---|---|---|---|---|
| | | | | | Проект: Четырёхкомнатная квартира | **M 1:25** |
| | Лист | № док. | Подпись | Дата | | |
| Дизайнер | Кырлан А.С. | | | 04.11.26 | Остров M_26 (пом. 6). Чертёж изделия | Стадия: П; Лист: Д_16; Листов: 120 |

## Ведомость отделки помещений (форма 1 прил. А ГОСТ 21.501-2018). Лист 1 из 3

| № | Наименование помещения | Потолок | | | Стены и перегородки | | | Низ стен (плинтус) | | | Пол | | Примечание |
|---|---|---|---|---|---|---|---|---|---|---|---|---|---|
| | | Вид отделки | Код цвета | S, м² | Вид отделки | Код цвета | S, м² | Вид отделки | Код цвета | L, м | Вид отделки | S, м² | |
| 1 | Зал<br>18,16 м² | ГКЛ по каркасу П113, отм. +2,500; +2,600; окраска, Tikkurila Anti-Reflex 2, глубокоматовая, 2 слоя, подготовка Q3 | Tikkurila F497 | 18,16 | Окраска, Tikkurila Optiva 5 Matt, матовая, 2 слоя, подготовка К3<br>Акцент — стена А: окраска, Tikkurila Optiva 5 Matt, матовая, 3 слоя, аналог: интерьерная краска, класс 2 по EN 13300, глубокоматовая/матовая, база С, подготовка К3 | Tikkurila F497<br>Tikkurila L481 | 25,94<br>13,55 | Плинтус МДФ h=80 мм, аналог: МДФ под окраску 80×16 мм | Tikkurila F497 | 16,6 | Инженерная доска, аналог: дуб натуральный брашированный, масло-воск, 14/4 мм, на клею; тип 1, отм. ЧП ±0,000 | 18,16 | Н стен 2500 (до потолка); колеруется в код стен, но по эмали на МДФ: сличать отдельным выкрасом на своей подложке (выкрас № 10); плинтус в цвет: стены |
| 2 | Ванная комната<br>5,57 м² | ГКЛВ по каркасу П113, отм. +2,500; окраска, Tikkurila Luja 7, матовая, 2 слоя, подготовка Q3 | Tikkurila F497 | 5,57 | Облицовка плиткой, аналог: керамогранит матовый, тон F497, 600×600×9 мм, клей С2 TE S1, затирка CG2WA | #F1F1EC | 22,35 | нет (облицовка от пола) | | | Аналог: керамогранит матовый R10, тон J484, 600×600×10 мм; тип 2, отм. ЧП −0,015 | 5,57 | Н стен 2515 (до потолка); тёплый пол; гидроизоляция обмазочная, 2 слоя, по всему помещению, с заведением на стены 200 мм; над ванной — до 2100 и 300 мм за борт (по пирогу пола); тест проливом и акт скрытых работ; облицовка от чистого пола до низа потолка; по ГКЛВ каркаса П113, влагостойкая окраска; Q3 |
| 3 | Тёмная комната<br>2,96 м² | ГКЛ по каркасу П113, отм. +2,600; окраска, Tikkurila Anti-Reflex 2, глубокоматовая, 2 слоя, подготовка Q3 | Tikkurila F497 | 2,96 | Окраска, Tikkurila Optiva 5 Matt, матовая, 2 слоя, подготовка К3 | Tikkurila F497 | 16,94 | Плинтус МДФ h=80 мм, аналог: МДФ под окраску 80×16 мм | Tikkurila F497 | 6,4 | Инженерная доска, аналог: дуб натуральный брашированный, масло-воск, 14/4 мм, на клею; тип 1, отм. ЧП ±0,000 | 2,96 | Н стен 2600 (до потолка); колеруется в код стен, но по эмали на МДФ: сличать отдельным выкрасом на своей подложке (выкрас № 10); плинтус в цвет: стены |
| 4 | Детская 1<br>17,51 м² | ГКЛ по каркасу П113, отм. +2,600; окраска, Tikkurila Anti-Reflex 2, глубокоматовая, 2 слоя, подготовка Q3 | Tikkurila F497 | 17,51 | Окраска, Tikkurila Joker, полуматовая, 2 слоя, подготовка К3 | Tikkurila F497 | 40,12 | Плинтус МДФ h=80 мм, аналог: МДФ под окраску 80×16 мм | Tikkurila F497 | 16,2 | Инженерная доска, аналог: дуб натуральный брашированный, масло-воск, 14/4 мм, на клею; тип 1, отм. ЧП ±0,000 | 17,51 | Н стен 2600 (до потолка); колеруется в код стен, но по эмали на МДФ: сличать отдельным выкрасом на своей подложке (выкрас № 10); плинтус в цвет: стены |
| 5 | Коридор<br>4,54 м² | ГКЛ по каркасу П113, отм. +2,600; окраска, Tikkurila Anti-Reflex 2, глубокоматовая, 2 слоя, подготовка Q3 | Tikkurila F497 | 4,54 | Окраска, Tikkurila Optiva 20 Semimatt, полуматовая, 2 слоя, подготовка К3 | Tikkurila J484 | 22,21 | Плинтус МДФ h=80 мм, аналог: МДФ под окраску 80×16 мм | Tikkurila J484 | 8,1 | Аналог: керамогранит матовый R10, тон V486, 600×600×10 мм; тип 3, отм. ЧП ±0,000 | 4,54 | Н стен 2600 (до потолка); колеруется в код стен, но по эмали на МДФ: сличать отдельным выкрасом на своей подложке (выкрас № 10); плинтус в цвет: стены |
| 6 | Кухня<br>15,19 м² | ГКЛ по каркасу П113, отм. +2,600; окраска, Tikkurila Luja 7, матовая, 2 слоя, подготовка Q3 | Tikkurila F497 | 15,19 | Окраска, Tikkurila Luja 7, полуматовая, 2 слоя, подготовка К3<br>Фартук кухни (стена А): облицовка керамогранитом, аналог: керамогранит матовый, тон F497, 600×600×9 мм, клей С2 TE S1, затирка CG2WA | Tikkurila F497<br>#F1F1EC | 34,48<br>1,11 | Плинтус МДФ h=80 мм, аналог: МДФ под окраску 80×16 мм | Tikkurila F497 | 13,8 | Инженерная доска, аналог: дуб натуральный брашированный, масло-воск, 14/4 мм, на клею; тип 4, отм. ЧП ±0,000 | 15,19 | Н стен 2600 (до потолка); гидроизоляция обмазочная, 2 слоя, с заведением на стены 200 мм (по пирогу пола); тест проливом и акт скрытых работ; влагостойкая полуматовая окраска (класс мокрого истирания 1 по EN 13300); категория К3 по СП 71.13330.2017, табл. 7.5; по ГКЛ каркаса П113, влагостойкая окраска; Q3 колеруется в код стен, но по эмали на МДФ: сличать отдельным выкрасом на своей подложке (выкрас № 10); плинтус в цвет: стены |

### Примечания

1. Ведомость продолжена на листе 2 из 3; итоги, сводка площадей и примечания — на последнем листе ведомости.

| | | | | | |
|---|---|---|---|---|---|
| | | | | | Проект: Четырёхкомнатная квартира |
| | Лист | № док. | Подпись | Дата | |
| Дизайнер | Кырлан А.С. | | | 04.11.26 | Ведомость отделки помещений. Лист 1 из 3 |

| Стадия | Лист | Листов |
|---|---|---|
| П | С1 | 120 |

## Ведомость отделки помещений (форма 1 прил. А ГОСТ 21.501-2018). Лист 2 из 3

| № | Наименование помещения | Потолок | | | Стены и перегородки | | | Низ стен (плинтус) | | | Пол | | Примечание |
|---|---|---|---|---|---|---|---|---|---|---|---|---|---|
| | | Вид отделки | Код цвета | S, м² | Вид отделки | Код цвета | S, м² | Вид отделки | Код цвета | L, м | Вид отделки | S, м² | |
| 7 | Прихожая-коридор<br>7,80 м² | ГКЛ по каркасу П113, отм. +2,600; окраска, Tikkurila Anti-Reflex 2, глубокоматовая, 2 слоя, подготовка Q3 | Tikkurila F497 | 7,80 | Окраска, Tikkurila Optiva 20 Semimatt, полуматовая, 2 слоя, подготовка К3 | Tikkurila J484 | 23,80 | Плинтус МДФ h=80 мм, аналог: МДФ под окраску 80×16 мм | Tikkurila J484 | 8,7 | Аналог: керамогранит матовый R10, тон V486, 600×600×10 мм; тип 3, отм. ЧП ±0,000 | 7,80 | Н стен 2600 (до потолка); колеруется в код стен, но по эмали на МДФ: сличать отдельным выкрасом на своей подложке (выкрас № 10); плинтус в цвет: стены |
| 8 | Гардеробная 2<br>1,29 м² | ГКЛ по каркасу П113, отм. +2,600; окраска, Tikkurila Anti-Reflex 2, глубокоматовая, 2 слоя, подготовка Q3 | Tikkurila F497 | 1,29 | Окраска, Tikkurila Optiva 5 Matt, матовая, 2 слоя, подготовка К3 | Tikkurila F497 | 8,65 | Плинтус МДФ h=80 мм, аналог: МДФ под окраску 80×16 мм | Tikkurila F497 | 3,3 | Инженерная доска, аналог: дуб натуральный брашированный, масло-воск, 14/4 мм, на клею; тип 1, отм. ЧП ±0,000 | 1,29 | Н стен 2600 (до потолка); колеруется в код стен, но по эмали на МДФ: сличать отдельным выкрасом на своей подложке (выкрас № 10); плинтус в цвет: стены |
| 9 | Детская 2<br>10,96 м² | ГКЛ по каркасу П113, отм. +2,600; окраска, Tikkurila Anti-Reflex 2, глубокоматовая, 2 слоя, подготовка Q3 | Tikkurila F497 | 10,96 | Окраска, Tikkurila Joker, полуматовая, 2 слоя, подготовка К3 | Tikkurila F497 | 29,08 | Плинтус МДФ h=80 мм, аналог: МДФ под окраску 80×16 мм | Tikkurila F497 | 11,8 | Инженерная доска, аналог: дуб натуральный брашированный, масло-воск, 14/4 мм, на клею; тип 1, отм. ЧП ±0,000 | 10,96 | Н стен 2600 (до потолка); колеруется в код стен, но по эмали на МДФ: сличать отдельным выкрасом на своей подложке (выкрас № 10); плинтус в цвет: стены |
| 10 | Санузел<br>1,31 м² | ГКЛВ по каркасу П113, отм. +2,500; окраска, Tikkurila Luja 7, матовая, 2 слоя, подготовка Q3 | Tikkurila F497 | 1,31 | Облицовка плиткой, аналог: керамогранит матовый, тон F497, 600×600×9 мм, клей C2 TE S1, затирка CG2WA | #F1F1EC | 10,46 | нет (облицовка от пола) | | | Аналог: керамогранит матовый R10, тон J484, 600×600×10 мм; тип 2, отм. ЧП −0,015 | 1,31 | Н стен 2515 (до потолка); тёплый пол; гидроизоляция обмазочная, 2 слоя, по всему помещению, с заведением на стены 200 мм (по пирогу пола); тест проливом и акт скрытых работ; облицовка от чистого пола до низа потолка; по ГКЛВ каркаса П113, влагостойкая окраска; Q3 |
| 11 | Гостиная<br>14,55 м² | ГКЛ по каркасу П113, отм. +2,600; окраска, Tikkurila Anti-Reflex 2, глубокоматовая, 2 слоя, подготовка Q3 | Tikkurila F497 | 14,55 | Окраска, Tikkurila Optiva 5 Matt, матовая, 2 слоя, подготовка К3<br>Акцент — стена А: окраска, Tikkurila Optiva 5 Matt, матовая, 3 слоя, аналог: интерьерная краска, класс 2 по EN 13300, глубокоматовая/матовая, база С, подготовка К3 | Tikkurila F497<br>Tikkurila L481 | 27,79<br>11,13 | Плинтус МДФ h=80 мм, аналог: МДФ под окраску 80×16 мм | Tikkurila F497 | 15,6 | Инженерная доска, аналог: дуб натуральный брашированный, масло-воск, 14/4 мм, на клею; тип 1, отм. ЧП ±0,000 | 14,55 | Н стен 2600 (до потолка); колеруется в код стен, но по эмали на МДФ: сличать отдельным выкрасом на своей подложке (выкрас № 10); плинтус в цвет: стены |
| 12 | Гардеробная 1<br>2,83 м² | ГКЛ по каркасу П113, отм. +2,600; окраска, Tikkurila Anti-Reflex 2, глубокоматовая, 2 слоя, подготовка Q3 | Tikkurila F497 | 2,83 | Окраска, Tikkurila Optiva 5 Matt, матовая, 2 слоя, подготовка К3 | Tikkurila F497 | 14,96 | Плинтус МДФ h=80 мм, аналог: МДФ под окраску 80×16 мм | Tikkurila F497 | 5,5 | Инженерная доска, аналог: дуб натуральный брашированный, масло-воск, 14/4 мм, на клею; тип 1, отм. ЧП ±0,000 | 2,83 | Н стен 2600 (до потолка); колеруется в код стен, но по эмали на МДФ: сличать отдельным выкрасом на своей подложке (выкрас № 10); плинтус в цвет: стены |
| 13 | Балкон 1<br>3,70 м² | ГКЛВ по каркасу П113, отм. +2,500; окраска, Tikkurila Luja 7, матовая, 2 слоя, подготовка Q3 | Tikkurila F497 | 3,70 | Окраска, Tikkurila Luja 7, полуматовая, 2 слоя, подготовка К3 | Tikkurila F497 | 16,51 | Плинтус из керамогранита h=80 мм, аналог: из керамогранита пола, подрезка 80 мм, верхняя кромка с запилом 45° | #B8AFA5 | 7,7 | Аналог: керамогранит матовый R11, тон V486, 600×600×10 мм; тип 5, отм. ЧП −0,030 | 3,70 | Н стен 2530 (до потолка); влагостойкая окраска по утеплённой стене; категория К3 по СП 71.13330.2017, табл. 7.5; по ГКЛВ каркаса П113, влагостойкая окраска; Q3 |

### Примечания

1. Ведомость продолжена на листе 3 из 3; итоги, сводка площадей и примечания — на последнем листе ведомости.

| | | | | | |
|---|---|---|---|---|---|
| | | | | | Проект: Четырёхкомнатная квартира |
| | Лист | № док. | Подпись | Дата | Ведомость отделки помещений. Лист 2 из 3 |
| Дизайнер | Кырлан А.С. | | | 04.11.26 | |

| Стадия | Лист | Листов |
|---|---|---|
| П | С2 | 120 |

## Ведомость отделки помещений (форма 1 прил. А ГОСТ 21.501-2018). Лист 3 из 3

| № | Наименование помещения | Потолок | | | Стены и перегородки | | | Низ стен (плинтус) | | | Пол | | Примечание |
|---|---|---|---|---|---|---|---|---|---|---|---|---|---|
| | | Вид отделки | Код цвета | S, м² | Вид отделки | Код цвета | S, м² | Вид отделки | Код цвета | L, м | Вид отделки | S, м² | |
| | **Итого** | | | **106,37** | | | **319,07** | | | **113,7** | | **106,37** | |

## Сводка площадей по материалам отделки

| Поверхность | Материал / код цвета | Серия | Площадь, м² |
|---|---|---|---|
| Потолок | Tikkurila F497 | Anti-Reflex 2 | 80,60 |
| Потолок | Tikkurila F497 | Luja 7 | 25,77 |
| Стены | Tikkurila F497 | Optiva 5 Matt | 94,28 |
| Стены | Tikkurila L481 | Optiva 5 Matt | 24,68 |
| Стены | облицовка плиткой 600×600×9 мм, #F1F1EC | аналог: керамогранит матовый, тон F497 | 32,81 |
| Стены | Tikkurila F497 | Joker | 69,20 |
| Стены | Tikkurila J484 | Optiva 20 Semimatt | 46,01 |
| Стены | Tikkurila F497 | Luja 7 | 50,99 |
| Фартук | облицовка керамогранитом 600×600×9 мм, #F1F1EC | аналог: керамогранит матовый, тон F497 | 1,11 |

## Примечания

1. Площади поверхностей — по чистым граням стен до отделки: стены = периметр × высоту от чистого пола помещения до низа потолка минус проёмы (облицовка плиткой — до верха облицовки); плинтус = периметр минус дверные проёмы; пол и потолок — по площади помещения. Количество плиток по раскладке. Площади помещений — с учётом всех частей помещения; откосы в площадь стен не входят.
2. Акцентные стены и фартук — отдельными строками, их площадь вычтена из основной отделки стен помещения; фартук — над нижними модулями кухни от столешницы до низа навесных шкафов, где шкафов нет — на 600 мм.
3. Плинтус — длина по периметру за вычетом дверных проёмов; примыкания к наличникам и встроенной мебели — по развёрткам.
4. Формат плитки — Ш×В×Т (ширина × высота в положении укладки × толщина), мм; на полу — вдоль стен А/В × вдоль стен Б/Г.
5. Коды цвета — по веерам производителей; колеровка каждой краски одной партией, проверка выкраса при свете D65 и при лампах проекта.
6. Уровни подготовки Q1–Q4 — система Knauf, не норма ГОСТ/СП; допуски поверхностей — по СП 71.13330.2017 (действующая редакция).
7. «аналог:» — изделие задано характеристиками, марку и артикул согласовать с заказчиком до закупки.
8. Плавающая стяжка по звукоизоляции: демпферная (кромочная) лента по контуру помещения и у стояков (СП 51.13330.2011, п. 9.11); плинтус крепится только к стене.

| | | | | | |
|---|---|---|---|---|---|
| | | | | | Проект: Четырёхкомнатная квартира |
| | Лист | № док. | Подпись | Дата | Ведомость отделки помещений. Лист 3 из 3 |
| Дизайнер | Кырлан А.С. | | | 04.11.26 | |

| Стадия | Лист | Листов |
|---|---|---|
| П | С3 | 120 |

| Поз. | Наименование и техническая характеристика | Тип, марка, обозначение документа | Код продукции | Поставщик | Ед. изм. | Кол. | Образец | Примечание |
|---|---|---|---|---|---|---|---|---|
| | **Лакокрасочные материалы** | | | | | | | |
| 1 | Краска интерьерная водно-дисперсионная акриловая для стен, матовая, класс мокрого истирания 2 по EN 13300, база A; цвет по вееру Tikkurila F497 «Paper», колеровка машинная | Tikkurila Optiva 5 Matt | | Tikkurila | л | 26,1 | | поз. К1 колерной карты; пом. 1, 3, 8, 11, 12; S = 94,3 м² × 2 сл. × 0,12 л/м² = 22,6 л, +10 % и 0,5 л на подкраску → ≥ 25,4 л; тара 2 × 9 л + 3 × 2,7 л |
| 2 | Краска интерьерная водно-дисперсионная акриловая для акцентных стен, матовая, класс мокрого истирания 2 по EN 13300, база C; цвет по вееру Tikkurila L481 «Silhouette», колеровка машинная | Tikkurila Optiva 5 Matt | | Tikkurila | л | 10,8 | | поз. К2 колерной карты; пом. 1, 11; S = 24,7 м² × 3 сл. × 0,12 л/м² = 8,9 л, +10 % и 0,5 л на подкраску → ≥ 10,3 л; тара 1 × 9 л + 2 × 0,9 л |
| 3 | Краска интерьерная водно-дисперсионная акриловая для потолков, глубокоматовая, класс мокрого истирания 2 по EN 13300, база A; цвет по вееру Tikkurila F497 «Paper», колеровка машинная | Tikkurila Anti-Reflex 2 | | Tikkurila | л | 22,5 | | поз. К3 колерной карты; пом. 1, 3, 4, 5, 7, 8, 9, 11, 12; S = 80,6 м² × 2 сл. × 0,12 л/м² = 19,3 л, +10 % и 0,5 л на подкраску → ≥ 21,8 л; тара 2 × 9 л + 1 × 2,7 л + 2 × 0,9 л |
| 4 | Краска интерьерная водно-дисперсионная акриловая для потолков, матовая, класс мокрого истирания 1 по EN 13300, база A; цвет по вееру Tikkurila F497 «Paper», колеровка машинная | Tikkurila Luja 7 | | Tikkurila | л | 8,1 | | поз. К5 колерной карты; пом. 2, 6, 10, 13; S = 25,8 м² × 2 сл. × 0,12 л/м² = 6,2 л, +10 % и 0,5 л на подкраску → ≥ 7,3 л; тара 3 × 2,7 л |
| 5 | Краска интерьерная водно-дисперсионная акриловая для стен, полуматовая, класс мокрого истирания 2 по EN 13300, база A; цвет по вееру Tikkurila F497 «Paper», колеровка машинная | Tikkurila Joker | | Tikkurila | л | 18,9 | | поз. К6 колерной карты; пом. 4, 9; S = 69,2 м² × 2 сл. × 0,12 л/м² = 16,6 л, +10 % и 0,5 л на подкраску → ≥ 18,8 л; тара 2 × 9 л + 1 × 0,9 л |
| 6 | Краска интерьерная водно-дисперсионная акриловая для стен, полуматовая, класс мокрого истирания 2 по EN 13300, база A; цвет по вееру Tikkurila J484 «Castle», колеровка машинная | Tikkurila Optiva 20 Semimatt | | Tikkurila | л | 13,5 | | поз. К7 колерной карты; пом. 5, 7; S = 46,0 м² × 2 сл. × 0,12 л/м² = 11,0 л, +10 % и 0,5 л на подкраску → ≥ 12,6 л; тара 1 × 9 л + 1 × 2,7 л + 2 × 0,9 л |
| 7 | Краска интерьерная водно-дисперсионная акриловая для стен, полуматовая, класс мокрого истирания 1 по EN 13300, база A; цвет по вееру Tikkurila F497 «Paper», колеровка машинная | Tikkurila Luja 7 | | Tikkurila | л | 14,4 | | поз. К9 колерной карты; пом. 6, 13; S = 51,0 м² × 2 сл. × 0,12 л/м² = 12,2 л, +10 % и 0,5 л на подкраску → ≥ 14,0 л; тара 1 × 9 л + 2 × 2,7 л |
| 8 | Акрилово-уретановая эмаль на водной основе, полуглянцевая в цвет Tikkurila F497 «Paper» — окраска плинтуса | аналог по характеристикам | | | л | 2,3 | | поз. К4; пом. 1, 3, 4, 6, 8, 9, 11, 12; L = 89,2 м, S = 8,6 м² × 2 сл. × 0,12 л/м² + 10 %; продукт подобрать в веере Tikkurila |
| 9 | Акрилово-уретановая эмаль на водной основе, полуглянцевая в цвет Tikkurila J484 «Castle» — окраска плинтуса | аналог по характеристикам | | | л | 0,5 | | поз. К8; пом. 5, 7; L = 16,8 м, S = 1,6 м² × 2 сл. × 0,12 л/м² + 10 %; продукт подобрать в веере Tikkurila |
| 10 | Грунтовка акриловая под окраску стен и потолков — из системы производителя краски | по системе краски | | | м² | 392 | | площадь окраски стен, акцентов и потолков; 1 слой перед окраской; расход — по ТУ грунтовки |



| | Лист | № док. | Подпись | Дата | Проект: Четырёхкомнатная квартира | | | |
|---|---|---|---|---|---|---|---|---|
| Дизайнер | Кырлан А.С. | | | 04.11.26 | Спецификация отделочных материалов | Стадия | Лист | Листов |
| | | | | | | П | С4 | 120 |

| Поз. | Наименование и техническая характеристика | Тип, марка, обозначение документа | Код продукции | Поставщик | Ед. изм. | Кол. | Образец | Примечание |
|---|---|---|---|---|---|---|---|---|
| | **Плитка и керамогранит** | | | | | | | |
| 11 | Керамогранит матовый R10, тон J484, 600.8×600.8 мм | аналог по характеристикам | | | м² | 10,47 | | шов 2 мм; Ванная комната, пол; Санузел, пол; по раскладке 26 шт (S = 6,88 м²), с запасом 29 шт |
| 12 | Керамогранит матовый, тон F497, 600.8×600.8 мм | аналог по характеристикам | | | м² | 63,17 | | шов 2 мм; Ванная комната, стены А–Г; Ванная комната, короб инсталляции; Санузел, стены А–Г; Санузел, короб инсталляции; по раскладке 157 шт (S = 34,22 м²), с запасом 175 шт |
| 13 | Керамогранит матовый R10, тон V486, 600.8×600.8 мм | аналог по характеристикам | | | м² | 15,88 | | шов 2 мм; Коридор, пол; Прихожая-коридор, пол; по раскладке 39 шт (S = 12,34 м²), с запасом 44 шт |
| 14 | Керамогранит матовый, тон F497, 600.8×600.8 мм | аналог по характеристикам | | | м² | 1,80 | | шов 2 мм; Кухня, фартук (ст. А); по раскладке 4 шт (S = 1,11 м²), с запасом 5 шт |
| 15 | Керамогранит матовый R11, тон V486, водопоглощение 0,5 % (BIa), противоскольжение R11, PEI IV | аналог по характеристикам | | | м² | 4,07 |  | 13. Балкон 1, пол; раскладка не выполнена — S = 3,70 м² + 10 %; клей и затирка — по раскладке |
| 16 | Плинтус из керамогранита пола, подрезка 80 мм, верхняя кромка с запилом 45° | аналог по характеристикам | | | м² | 8,46 |  | 13. Балкон 1, стены; раскладка не выполнена — S = 7,69 м² + 10 %; клей и затирка — по раскладке |
| | **Напольные покрытия** | | | | | | | |
| 17 | Дуб натуральный брашированный, масло-воск, 14/4 мм, эмиссия E1, укладка на клей | аналог по характеристикам | | | м² | 89,3 |  | пом. 1, 3, 4, 6, 8, 9, 11, 12; S = 83,45 м² + 7 % (прямая укладка); к заказу — кратно упаковке |
| 18 | Клей для паркета и инженерной доски, эластичный (СМП / полиуретановый) | по рекомендации производителя доски | | | м² | 84 | | площадь приклейки; расход и шпатель — по ТУ клея |
| | **Погонажные изделия** | | | | | | | |
| 19 | Плинтус МДФ под окраску 80×16 мм, крепление к стене, окраска в цвет Tikkurila F497 | аналог по характеристикам | | | м | 99 | | пом. 1, 3, 4, 6, 8, 9, 11, 12; L = 89,2 м (периметр без дверных проёмов) + 10 % на подрезку; в штуках — по длине планки |
| 20 | Плинтус МДФ под окраску 80×16 мм, крепление к стене, окраска в цвет Tikkurila J484 | аналог по характеристикам | | | м | 19 | | пом. 5, 7; L = 16,8 м (периметр без дверных проёмов) + 10 % на подрезку; в штуках — по длине планки |
| 21 | Плинтус из керамогранита пола, подрезка 80 мм, верхняя кромка с запилом 45°, h = 80 мм, крепление к стене | аналог по характеристикам | | | м | 9 | | пом. 13; L = 7,7 м (периметр без дверных проёмов) + 10 % на подрезку; в штуках — по длине планки |
| | **Смеси и материалы для облицовки** | | | | | | | |
| 22 | Затирка для швов плитки, класс CG2WA по EN 13888 | аналог: Mapei Ultracolor 133 | | аналог: | кг | 5,7 | | по раскладке (a+b)/(a·b) × шов × t × 1,6 + 10 %; в т. ч. 0,1 кг — позиции раскладки без марки |
| 23 | Клей плиточный C2 TE S1 по EN 12004, слой 5 мм | аналог: Litokol K80 Eco | | аналог: | кг | 434 | | 18 меш. по 25 кг; 1,5 кг/м² на 1 мм слоя + 10 %; в т. ч. 10 кг — позиции раскладки без марки |
| 24 | Гидроизоляция обмазочная мокрых зон: пол, стены по периметру, зоны замачивания; 2 слоя с армирующей лентой в углах | аналог по характеристикам | | | м² | 16,2 | | площадь по листу раскладки плитки + 10 %; расход смеси — по ТУ |
| 25 | Лента демпферная по периметру пола из плитки | аналог по характеристикам | | | м | 29,1 | | периметр без дверных проёмов + 10 % |

## Примечания

1. Количества — из геометрии проекта: площади поверхностей по чистым граням стен до отделки (те же, что в ведомости отделки и колерной карте), плитка, клей и затирка — по раскладке плиточника; в графе «Кол.» — к заказу, с запасом.
2. Краска: расход 0,12 л/м² на слой в 2 слоя, если по ТУ не задан иной; запас 10 % и 0,5 л на подкраску каждого кода. Один код — одна партия, колеровка машинная в колеровочном центре бренда; в заказ — только после утверждения выкраса (колерная карта). Фасовка — по каталогу бренда на дату выпуска; к заказу — не меньше расчётного объёма.
3. «Аналог по характеристикам» — допускается изделие другого производителя с характеристиками не ниже указанных, по согласованию с автором проекта.
4. Графы «Код продукции» и «Масса 1 ед.» не заполнены: коды по классификатору продукции не присвоены, масса единицы до 25 кг (ГОСТ 21.110-2013).
5. Грунтовка и клей для доски указаны площадью обработки; объём — по ТУ выбранного продукта.

| | | | | | |
|---|---|---|---|---|---|
| | | | | | Проект: Четырёхкомнатная квартира |
| | Лист | № док. | Подпись | Дата | |
| Дизайнер | Кырлан А.С. | | | 04.11.26 | Спецификация отделочных материалов |

| Стадия | Лист | Листов |
|---|---|---|
| П | С5 | 120 |

## Список покупок: материалы для магазина

| № | Что купить | Артикул или характеристика | Нужно с запасом | Брать в магазине | Фасовка | Уточнить в магазине | Помещения | Кто покупает |
|---|---|---|---|---|---|---|---|---|
| **Покрытия полов и облицовка** | | | | | | | | |
| 1 | Инженерная доска (дуб натуральный, рабочий слой 4 мм, эмиссия E1, прямая укладка) | по характеристике: дуб натуральный брашированный, масло-воск, 14/4 мм | 89,94 м² | 90 м² | | уточнить в магазине: м² в упаковке | 1, 3, 4, 6, 8, 9, 11, 12 | по проекту |
| 2 | Клей для паркетной и инженерной доски (эластичный, по ТУ изготовителя доски) | на выбор бригады по проекту | 84,06 м² | | | уточнить в магазине: расход и фасовку — по выбранному продукту | | бригада |
| 3 | Керамогранит 600,8×600,8 мм матовый R10, тон J484 | керамогранит матовый R10, тон J484 | 29 шт | 29 шт | | уточнить в магазине: штук в коробке | 2, 10 | по проекту |
| 4 | Керамогранит 600,8×600,8 мм матовый, тон F497 | по характеристике: керамогранит матовый, тон F497 | 178 шт | 180 шт | | уточнить в магазине: штук в коробке | 2, 6, 10 | по проекту |
| 5 | Керамогранит 600,8×600,8 мм матовый R10, тон V486 | керамогранит матовый R10, тон V486 | 43 шт | 44 шт | | уточнить в магазине: штук в коробке | 5, 7 | по проекту |
| 6 | Керамогранит, R11 | по характеристике: керамогранит матовый R11, тон V486, 600×600×10 мм | 4,11 м² | 4,2 м² | | уточнить в магазине: м² в коробке | 13 | по проекту |
| **Сухие смеси и гидроизоляция** | | | | | | | | |
| 7 | Клей плиточный цементный класса C2 TE S1 (ГОСТ Р 56387-2018) | аналог: Litokol K80 Eco или аналог | 433,74 кг | 18 меш. | мешок 25 кг | | | по проекту |
| 8 | Затирка цементная класса CG2WA, цвет — по колерной карте | аналог: Mapei Ultracolor 133 или аналог | 5,69 кг | 3 упак. | упак. 2 кг | | | по проекту |
| 9 | Гидроизоляция обмазочная полимерная, 2 слоя, лента в углах, манжеты на выводах | на выбор бригады по проекту | 16,21 м² | | | уточнить в магазине: расход и фасовку — по выбранному продукту | 2, 10 | бригада |
| 10 | Лента демпферная по периметру пола из плитки | на выбор бригады по проекту | 29,06 м | 30 м | | уточнить в магазине: фасовку | | бригада |
| 11 | Смесь цементно-песчаная для стяжки М200 (55 мм, 53 мм) | на выбор бригады по проекту | 5,55 м³ | | | уточнить в магазине: расход и фасовку — по выбранному продукту | | бригада |
| 12 | Смесь штукатурная гипсовая для машинного и ручного нанесения по маякам, слой до 10 мм | на выбор бригады по проекту | 350,99 м² | | | уточнить в магазине: расход и фасовку — по выбранному продукту | 1, 2, 3, 4, 5, 6, 7, 8, 9, 10, 11, 12, 13 | бригада |
| **Короба из ГКЛВ** | | | | | | | | |
| 13 | Лист ГКЛВ 12,5 мм, 2500 × 1200 мм, обшивка коробов в 2 слоя | на выбор бригады по проекту | 6,86 м² | 3 лист. | лист 3,00 м² | | 2, 10 | бригада |
| 14 | Профиль стальной оцинкованный 27 × 28 мм: каркас коробов (стойки и направляющие) | на выбор бригады по проекту | 16,69 м | 6 шт | хлыст 3 м | | | бригада |
| **Слаботочные сети** | | | | | | | | |
| 15 | Кабель коаксиальный RG-6 (75 Ом) к розеткам ТВ | на выбор бригады по проекту | 14,5 м | 15 м | | уточнить в магазине: длину бухты | | бригада |
| 16 | Кабель U/UTP кат. 6 (LAN, Wi-Fi и камеры по PoE) | на выбор бригады по проекту | 72,7 м | 73 м | | уточнить в магазине: длину бухты | | бригада |
| 17 | Гофротруба Ø20 для слаботочных линий, отдельно от силовых | на выбор бригады по проекту | 78,5 м | 79 м | | уточнить в магазине: длину бухты | | бригада |
| 18 | Розетка компьютерная RJ45, кат. 6, с рамкой и подрозетником | на выбор бригады по проекту | 4 шт | 4 шт | шт | | | бригада |
| 19 | Розетка телевизионная (коаксиальная) с рамкой и подрозетником | на выбор бригады по проекту | 1 шт | 1 шт | шт | | | бригада |
| 20 | Щит слаботочный ЩС: корпус, DIN-рейка, розетки 220 В | на выбор бригады по проекту | 1 шт | 1 шт | шт | | | бригада |
| 21 | Патч-панель, портов не менее 6 | на выбор бригады по проекту | 1 шт | 1 шт | шт | | | бригада |

| | | | | | | |
|---|---|---|---|---|---|---|
| | | | | | Проект: Четырёхкомнатная квартира | |
| | Лист | № док. | Подпись | Дата | | |
| Дизайнер | Кырлан А.С. | | | 04.11.26 | Список покупок | Стадия: П; Лист: С6; Листов: 120 |

## Список покупок: материалы для магазина (продолжение)

| № | Что купить | Артикул или характеристика | Нужно с запасом | Брать в магазине | Фасовка | Уточнить в магазине | Помещения | Кто покупает |
|---|---|---|---|---|---|---|---|---|
| **Лакокрасочные материалы** | | | | | | | | |
| 22 | Краска интерьерная акриловая, матовая, класс истирания 2 | Tikkurila Optiva 5 Matt L481 «Silhouette» | 9,77 л | 4 банк. | банка 2,7 л | | 1, 11 | по проекту |
| 23 | Краска интерьерная акриловая, матовая, класс истирания 2 | Tikkurila Optiva 5 Matt F497 «Paper» | 24,89 л | 10 банк. | банка 2,7 л | | 1, 3, 8, 11, 12 | по проекту |
| 24 | Краска интерьерная акриловая, глубокоматовая, класс истирания 2 | Tikkurila Anti-Reflex 2 F497 «Paper» | 21,27 л | 8 банк. | банка 2,7 л | | 1, 3, 4, 5, 7, 8, 9, 11, 12 | по проекту |
| 25 | Краска интерьерная акриловая, матовая, класс истирания 1 | Tikkurila Luja 7 F497 «Paper» | 6,8 л | 3 банк. | банка 2,7 л | | 2, 6, 10, 13 | по проекту |
| 26 | Краска интерьерная акриловая, полуматовая, класс истирания 2 | Tikkurila Joker F497 «Paper» | 18,27 л | 7 банк. | банка 2,7 л | | 4, 9 | по проекту |
| 27 | Краска интерьерная акриловая, полуматовая, класс истирания 2 | Tikkurila Optiva 20 Semimatt J484 «Castle» | 12,14 л | 5 банк. | банка 2,7 л | | 5, 7 | по проекту |
| 28 | Краска интерьерная акриловая, полуматовая, класс истирания 1 | Tikkurila Luja 7 F497 «Paper» | 13,46 л | 5 банк. | банка 2,7 л | | 6, 13 | по проекту |
| 29 | Шпаклёвка финишная полимерная под окраску (стены и потолки, Q3) | на выбор бригады по проекту | 430,68 м² | | | уточнить в магазине: расход и фасовку — по выбранному продукту | | бригада |
| 30 | Грунтовка акриловая глубокого проникновения, 2 слоя | на выбор бригады по проекту | 468 м² | | | уточнить в магазине: расход и фасовку — по выбранному продукту | | бригада |
| **Погонажные изделия и потолки** | | | | | | | | |
| 31 | Плинтус напольный МДФ под покраску, h=80 мм, крепление к стене | по характеристике: плинтус МДФ под окраску 80×16 мм | 116,56 м.п. | 49 шт | хлыст 2,4 м | | 1, 3, 4, 5, 6, 7, 8, 9, 11, 12 | по проекту |
| 32 | Керамогранит на плинтус: полосы h=80 мм из плитки пола, кромка с запилом 45° | по характеристике: плинтус из керамогранита пола, подрезка 80 мм, верхняя кромка с запилом 45° | 0,71 м² | 0,71 м² | | уточнить в магазине: м² в коробке | 13 | по проекту |
| 33 | Потолок подвесной ГКЛ/ГКЛВ по каркасу Knauf П113: листы, профили, подвесы, лента, шпаклёвка швов | Knauf П113 | 106,37 м² | | | уточнить в магазине: расход и фасовку — по выбранному продукту | | по проекту |
| **Инженерные изделия** | | | | | | | | |
| 34 | Мат нагревательный электрический для тёплого пола под плитку, с холодным концом и муфтой | на выбор бригады по проекту | 1,67 м² | | | уточнить в магазине: расход и фасовку — по выбранному продукту | 2, 10 | по проекту |
| 35 | Терморегулятор тёплого пола с выносным датчиком пола, монтаж в подрозетник | на выбор бригады по проекту | 2 шт | 2 шт | шт | | | по проекту |

## Примечания


1. «Нужно с запасом» — расход по чертежам и раскладке плюс запас на подрезку и подкраску; «Брать в магазине» — то же количество в единицах, которыми продают (банки, мешки, упаковки, листы, штуки, литры).
2. «Уточнить в магазине» — фасовки этого товара в проекте нет: спросите у продавца, сколько в упаковке, и возьмите целое число упаковок не меньше «Нужно с запасом».
3. Плитку, доску и краску одного цвета берите одной партией (один калибр и тон на помещение) и сохраните чек и номер партии до конца ремонта.
4. «По характеристике» — артикул не выбран: подойдёт любой товар с этими свойствами, согласуйте его с дизайнером до покупки. «Бригада» материал выбирает и закупает бригада по своей технологии.
5. Помещения: 1 — Зал; 2 — Ванная комната; 3 — Тёмная комната; 4 — Детская 1; 5 — Коридор; 6 — Кухня; 7 — Прихожая-коридор; 8 — Гардеробная 2; 9 — Детская 2; 10 — Санузел; 11 — Гостиная; 12 — Гардеробная 1; 13 — Балкон 1; «—» — материал для нескольких помещений, расход по месту.



| | | | | | |
|---|---|---|---|---|---|
| | | | | | Проект: Четырёхкомнатная квартира |
| | Лист | № док. | Подпись | Дата | |
| Дизайнер | Кырлан А.С. | | | 04.11.26 | Список покупок (окончание) |
| | | | | | Стадия: П; Лист: С7; Листов: 120 |


### 1 Порог 15 мм: мокрая зона — смежное помещение (М 1:5)

Применение: двери

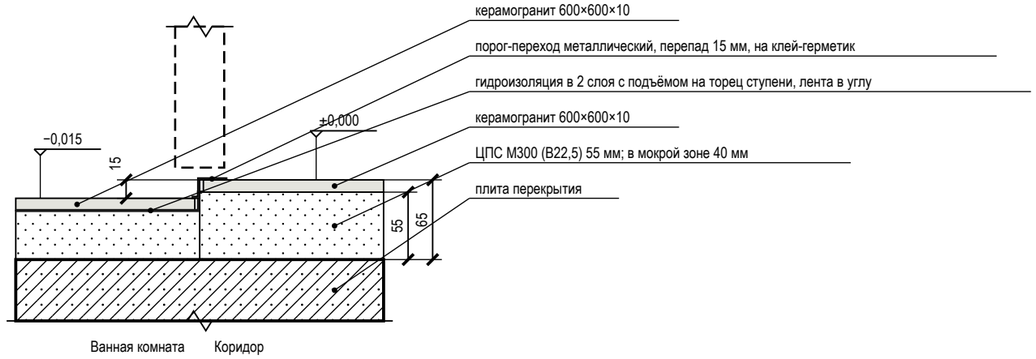



### 2 Стык покрытий пола Т-профилем без перепада (М 1:5)

Применение: проёмы 3↔5, 4↔5, 6↔7, 7↔8, 8↔7, 9↔7

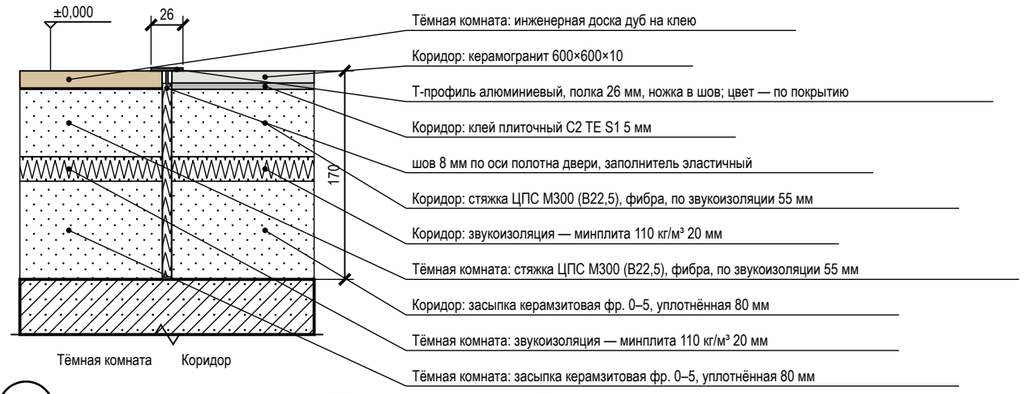



### 3 Короб стояков К1-1, В1-1, Т3-1 с люком и звукоизоляцией (М 1:20)

Применение: пом. 9

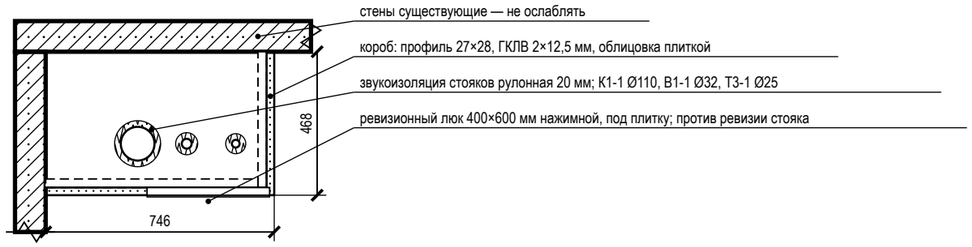



### 4 Гидроизоляция санузла: заход на стены 200 мм, примыкание ванны (М 1:20)

Применение: пом. 2, 10

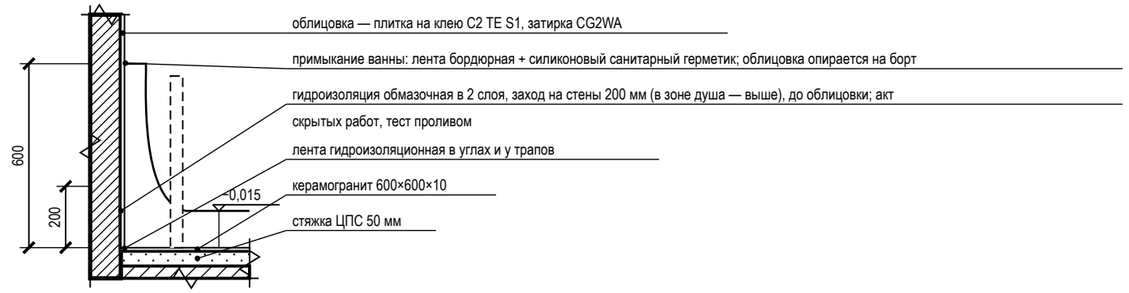



### 5 Плинтус МДФ 80×16 мм у окрашенной стены по доске (ламинату) (М 1:10)

Применение: пом. 1, 3, 4, 6, 8, 9, 11, 12

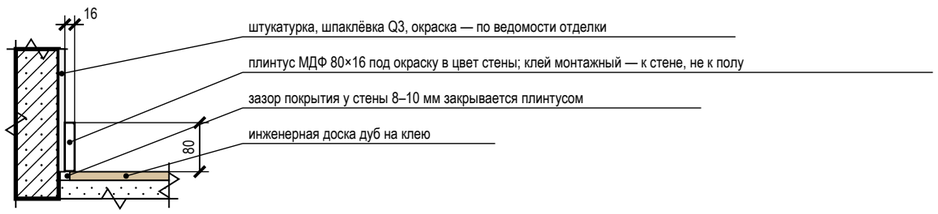


### 6 Плинтус МДФ 80×16 мм у окрашенной стены по керамограниту (плитке) (М 1:10)

Применение: пом. 5, 7

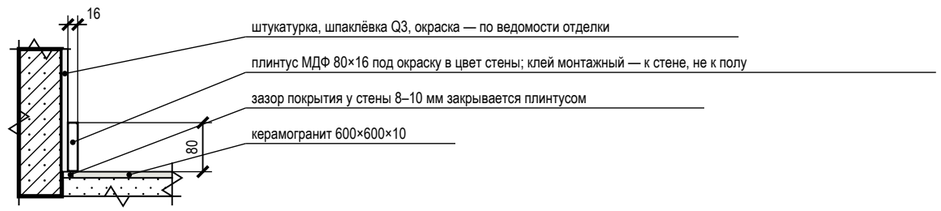


## Условные обозначения

- железобетон (плита, стены) — условно: конструкция не установлена
- кладка, перегородка — условно: конструкция не установлена
- стяжка, раствор
- гипсокартон ГКЛВ
- звукоизоляция, эластичный заполнитель
- плитка, керамогранит на клею
- инженерная доска (покрытие пола)
- металлический профиль (порог, Т-профиль, короб двери)
- гидроизоляция (обмазочная, лента)

## Примечания

1. Узлы — типовые решения проекта для мест, отмеченных выносками на листе схемы расположения развёрток и узлов; размеры — в мм, отметки — в м от ±0,000.
2. Узлы с гидроизоляцией, закладными и коробами скрытого монтажа принимаются по актам скрытых работ до закрытия отделкой; гидроизоляция — после теста проливом (24 ч).
3. Марки изделий (порог, Т-профиль, короб скрытой двери, люк) — по спецификациям; замена — на аналог с теми же габаритами по согласованию с автором проекта.
4. Материал плиты перекрытия и стен в узлах показан условно (железобетон, кладка): конструкция дома не установлена — крепёж, анкеры и толщины слоёв уточняются после обследования (до него — по допущениям общих указаний).

| | | | | | |
|---|---|---|---|---|---|
| | | | | | Проект: Четырёхкомнатная квартира |
| | Лист | № док. | Подпись | Дата | |
| Дизайнер | Кырлан А.С. | | | 04.11.26 | Узлы |

| Стадия | Лист | Листов |
|---|---|---|
| П | С8 | 120 |

выпуск 04.11.2026 № b23f08ad9b · стр. 120 из 120