
ПРЕДВАРИТЕЛЬНО · не для производства работ · открыто пунктов: 8 (реестр — л. 6, 7)

LINEA

ДИЗАЙН-ПРОЕКТ ИНТЕРЬЕРА

Квартира 101 м²

ретро с авторской мебелью

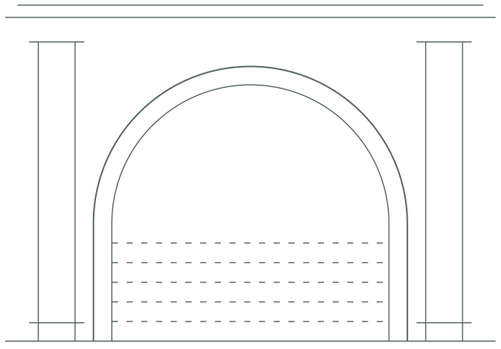

ПАЛИТРА ОТДЕЛКИ

F&B No. 291	NCS S 0502-Y	F&B No. 289	F&B No. 255	NCS S 1005-Y20
58 %	29 %	10 %	3 %	текстиль, декор

АВТОР ПРОЕКТА

Кырлан Александр Сергеевич

Ноябрь 2026



Квартира сверху · схематичная модель по плану

ОБЩАЯ ПЛОЩАДЬ	ПОМЕЩЕНИЙ	СТАДИЯ	ШИФР	ОСНОВА
100,72 м²	11, из них жилых 4	Рабочий проект · предварительно	ГД-2026-009-АИ	план заказчика, без обмера

Изм.	Кол.уч	Лист	№ док.	Подп.	Дата
Разраб.		Кырлан А.С.			04.11.26
Пров.					
ГИП					
Н. контр.					
Утв.					

ГД-2026-009-АИ

Квартира 103 м²

Общая площадь 100,72* м² · * размеры со скана, не замерены (реестр — л. 6, 7, К-1)

Дизайн-проект интерьера

Стадия	Лист	Листов
РП	1	120

Титульный лист

М б/м

Кырлан Александр Сергеевич

выпуск 04.11.2026 № 20cec94f32 · стр. 1 из 130

Общие данные

ПРЕДВАРИТЕЛЬНО · не для производства работ · открыто пунктов: 8 (реестр — л. 6, 7)

Комплект ГД-2026-009-АИ · Квартира 103 м² · ретро с авторской мебелью

Допущения и предложения на листе. См. лист открытых вопросов (лист 6).

Ведомость рабочих чертежей основного комплекта ГД-2026-009-АИ

Лист	Наименование	Примечание
1	Титульный лист	
2	Общие данные	
3	Общие данные	
4	Общие данные	
5	Общие данные	
6	Открытые вопросы, принятые допущения и конфликты. Лист 1 из 2	
7	Открытые вопросы, принятые допущения и конфликты. Лист 2 из 2	
8	Задание на контрольный обмер и обследование. Лист 1 из 3	
9	Задание на контрольный обмер и обследование. Лист 2 из 3	
10	Задание на контрольный обмер и обследование. Лист 3 из 3	
11	График закупок и работ. Лист 1 из 3	
12	График закупок и работ. Лист 2 из 3	
13	График закупок и работ. Лист 3 из 3	
14	Обмерный план	
15	План демонтажа и монтажа перегородок	
16	План дверей	
17	Ведомость заполнения проёмов	
18	Концепция интерьера	
19	План расстановки мебели	
20	Спецификация мебели и оборудования	
21	Спецификация мебели и оборудования (продолжение)	
22	Спецификация мебели и оборудования (продолжение)	
23	План розеток и электровыводов	
24	План освещения	
25	План выключателей и схема включения	
26	Ведомость электроточек и изделий	
27	Ведомость электроточек и изделий (продолжение)	
28	Однолинейная схема щита	
29	План принципиальных трасс	
30	План слаботочных сетей	

Ведомость рабочих чертежей основного комплекта ГД-2026-009-АИ (продолжение)

Лист	Наименование	Примечание
31	План вентиляции	
32	План отопления	
33	План выводов сантехники	
34	Схема разводки водопровода и канализации	
35	Аксонометрическая схема В1 (холодное водоснабжение)	
36	Аксонометрическая схема Т3 (горячее водоснабжение)	
37	Аксонометрическая схема К1 (канализация)	
38	Развёртки мокрых зон: выводы ВК. Кухня	
39	Развёртки мокрых зон: выводы ВК. Ванная	
40	Развёртки мокрых зон: выводы ВК. Постирочная	
41	Развёртки мокрых зон: выводы ВК. Ванная мастер	
42	Спецификация сантехнического оборудования	
43	Техническое задание на подбор светильников	
44	Техническое задание на подбор светильников (продолжение)	
45	План потолков	
46	Разрезы и узлы потолков	
47	Разрезы и узлы потолков (продолжение)	
48	Сечения потолков М 1:10	
49	Раскладка плитки. Планы полов	
50	Раскладка плитки. Прихожая-холл	
51	Раскладка плитки. Ванная. Развёртки стен	
52	Раскладка плитки. Ванная мастер. Развёртки стен	
53	План полов	

Общие указания — лист 5: ±0,000 — чистый пол; несущие конструкции и сети дома — по отдельному проекту; скрытые работы — по актам. Открытые вопросы и допущения — листы 6, 7.

Изм.	Кол.уч	Лист	№ док.	Подп.	Дата	ГД-2026-009-АИ		
						Квартира 103 м²		
						Общая площадь 100,72* м² · * размеры со скана, не замерены (реестр — л. 6, 7, К-1)		
Разраб.		Кырлан А.С.			04.11.26	Дизайн-проект интерьера	Стадия: РП	Лист: 2 / Листов: 120
Пров.								
ГИП								
Н. контр.						Общие данные	Кырлан Александр Сергеевич	
Утв.						М б/м		

Общие данные

ПРЕДВАРИТЕЛЬНО · не для производства работ · открыто пунктов: 8 (реестр — л. 6, 7)

Допущения и предложения на листе. См. лист открытых вопросов (лист 6).

Ведомость рабочих чертежей основного комплекта ГД-2026-009-АИ (продолжение)

Лист	Наименование	Примечание
54	Ведомость отделки помещений. Лист 1 из 3	
55	Ведомость отделки помещений. Лист 2 из 3	
56	Ведомость отделки помещений. Лист 3 из 3	
57	Колерная карта	
58	Колерная карта	
59	Спецификация отделочных материалов	
60	Спецификация отделочных материалов	
61	Концепция декора и визуализации	
62	План текстиля и декора	
63	Шторы и карнизы	
64	Ведомость текстиля	
65	Ведомость декора. Схемы развески	
66	Встроенная мебель. Схема расположения	
67	Система хранения Кл1	
68	Шкаф-купе П1	
69	Система хранения Пс1	
70	Шкаф распашной С2	
71	Шкаф распашной М4	
72	Кухня (пом. 5). Развёртка гарнитура	
73	Кухня (пом. 5). Монтажная схема	
74	Кухня (пом. 5). Развёртка гарнитура	
75	Кухня (пом. 5). Монтажная схема	
76	Шкафы. Монтажная схема	
77	Ведомости изделий, техники и фурнитуры	
78	Реестр марок отделки и позиций альбома	
79	Схема расположения развёрток и узлов	
80	Развёртки стен А, Б. Кабинет-библиотека (пом. 1)	
81	Развёртки стен В, Г. Кабинет-библиотека (пом. 1)	
82	Развёртки стен. Кладовая (пом. 2)	
83	Развёртка стены А. Гостиная-столовая (пом. 3)	

Ведомость рабочих чертежей основного комплекта ГД-2026-009-АИ (продолжение)

Лист	Наименование	Примечание
84	Привязки электроточек, стена А. Гостиная-столовая (пом. 3)	
85	Развёртка стены Б. Гостиная-столовая (пом. 3)	
86	Развёртка стены В. Гостиная-столовая (пом. 3)	
87	Развёртка стены Г. Гостиная-столовая (пом. 3)	
88	Развёртка стены А. Прихожая-холл (пом. 4)	
89	Развёртка стены Б. Прихожая-холл (пом. 4)	
90	Развёртка стены В. Прихожая-холл (пом. 4)	
91	Развёртка стены Г. Прихожая-холл (пом. 4)	
92	Развёртки стен Б, В. Кухня (пом. 5), кухонный фронт	
93	Привязки электроточек и выводов ВК, стена Б. Кухня (пом. 5)	
94	Развёртки стен А, Г. Кухня (пом. 5)	
95	Развёртки стен А, Б, В. Ванная (пом. 6)	
96	Развёртка стены Г. Ванная (пом. 6)	
97	Привязки электроточек и выводов ВК, стена Г. Ванная (пом. 6)	
98	Развёртки стен. Постирочная (пом. 7)	
99	Развёртки стен А, Б. Спальня 2 (пом. 8)	
100	Развёртка стены В. Спальня 2 (пом. 8)	
101	Развёртка стены Г. Спальня 2 (пом. 8)	
102	Развёртка стены А. Коридор (пом. 9)	
103	Развёртка стены Б. Коридор (пом. 9)	
104	Развёртка стены В. Коридор (пом. 9)	
105	Развёртка стены А. Спальня мастер (пом. 10)	
106	Привязки электроточек, стена А. Спальня мастер (пом. 10)	

Общие указания — лист 5: ±0,000 — чистый пол; несущие конструкции и сети дома — по отдельному проекту; скрытые работы — по актам. Открытые вопросы и допущения — листы 6, 7.

Изм.	Кол.уч	Лист	№ док.	Подп.	Дата
Разраб.		Кырлан А.С.			04.11.26
Пров.					
ГИП					
Н. контр.					
Утв.					

ГД-2026-009-АИ

Квартира 103 м²

Общая площадь 100,72* м² · * размеры со скана, не замерены (реестр — л. 6, 7, К-1)

Дизайн-проект интерьера

Стадия	Лист	Листов
РП	3	120

Общие данные

М б/м

Кырлан Александр Сергеевич

выпуск 04.11.2026 № 20cec94f32 · стр. 3 из 130

Общие данные

Комплект ГД-2026-009-АИ · лист 3 общих данных (продолжение)

Ведомость рабочих чертежей основного комплекта ГД-2026-009-АИ (продолжение)

Лист	Наименование	Примечание
107	Развёртка стены Б. Спальня мастер (пом. 10)	
108	Развёртки стен В, Г1. Спальня мастер (пом. 10)	
109	Развёртка стены Г2. Спальня мастер (пом. 10)	
110	Развёртки стен А, Б, В. Ванная мастер (пом. 11)	
111	Привязки электроточек и выводов ВК, стена А. Ванная мастер (пом. 11)	
112	Развёртка стены Г. Ванная мастер (пом. 11)	
113	Узлы	
114	Ведомость объёмов работ	
115	Ведомость объёмов работ (продолжение)	
116	Ведомость объёмов работ (окончание)	
117	Спецификация материалов	
118	Спецификация материалов (окончание)	
119	Смета ориентировочная	
120	Смета ориентировочная (окончание)	

Ведомость ссылочных и прилагаемых документов

Обозначение	Наименование	Примечание
	Ссылочные документы	
ГОСТ 21.201-2011	СПДС. Условные графические изображения элементов зданий, сооружений и конструкций	
ГОСТ 21.205-2016	СПДС. Условные обозначения элементов санитарно-технических систем	
ГОСТ 21.210-2014	СПДС. Изображения условные графические электрооборудования и проводок на планах	
ГОСТ 2.306-68	ЕСКД. Обозначения графические материалов и правила их нанесения на чертежах	
	Прилагаемые документы	
ГД-2026-009-АИ.В1	Визуализация. Вид сверху (3D): планировка с мебелью, текстилем и декором	альбом визуализаций
ГД-2026-009-АИ.В2	Визуализация. Интерьер: Ванная (пом. 6), стена Б	
ГД-2026-009-АИ.В3	Визуализация. Интерьер: Ванная (пом. 6), стена В	
ГД-2026-009-АИ.В4	Визуализация. Интерьер: Ванная (пом. 6), стена Г	
ГД-2026-009-АИ.В5	Визуализация. Интерьер: Ванная мастер (пом. 11), общий вид	

Общие указания — лист 5: ±0,000 — чистый пол; несущие конструкции и сети дома — по отдельному проекту; скрытые работы — по актам. Открытые вопросы и допущения — листы 6, 7.

Ведомость ссылочных и прилагаемых документов (продолжение)

Обозначение	Наименование	Примечание
ГД-2026-009-АИ.В6	Визуализация. Интерьер: Спальня 2 (пом. 8), стена А	
ГД-2026-009-АИ.В7	Визуализация. Интерьер: Спальня 2 (пом. 8), стена Б	
ГД-2026-009-АИ.В8	Визуализация. Интерьер: Спальня 2 (пом. 8), стена Г	
ГД-2026-009-АИ.В9	Визуализация. Интерьер: Спальня мастер (пом. 10), стена А	
ГД-2026-009-АИ.В10	Визуализация. Интерьер: Спальня мастер (пом. 10), стена Б	
ГД-2026-009-АИ.В11	Визуализация. Интерьер: Спальня мастер (пом. 10), стена В	
ГД-2026-009-АИ.В12	Визуализация. Интерьер: Спальня мастер (пом. 10), стена Г	
ГД-2026-009-АИ.В13	Визуализация. Интерьер: Коридор (пом. 9), стена Б	
ГД-2026-009-АИ.В14	Визуализация. Интерьер: Прихожая-холл (пом. 4), стена А	
ГД-2026-009-АИ.В15	Визуализация. Интерьер: Прихожая-холл (пом. 4), стена Б	
ГД-2026-009-АИ.В16	Визуализация. Интерьер: Кухня (пом. 5), стена Б	
ГД-2026-009-АИ.В17	Визуализация. Интерьер: Кухня (пом. 5), стена В	
ГД-2026-009-АИ.В18	Визуализация. Интерьер: Гостиная-столовая (пом. 3), стена А	
ГД-2026-009-АИ.В19	Визуализация. Интерьер: Гостиная-столовая (пом. 3), стена Б	
ГД-2026-009-АИ.В20	Визуализация. Интерьер: Гостиная-столовая (пом. 3), стена В	
ГД-2026-009-АИ.В21	Визуализация. Интерьер: Гостиная-столовая (пом. 3), стена Г	
ГД-2026-009-АИ.В22	Визуализация. Интерьер: Кабинет-библиотека (пом. 1), стена А	
ГД-2026-009-АИ.В23	Визуализация. Интерьер: Кабинет-библиотека (пом. 1), стена Б	
ГД-2026-009-АИ.В24	Визуализация. Интерьер: Кабинет-библиотека (пом. 1), стена Г	
ГД-2026-009-АИ.В25	Визуализация. Интерьер: Постирочная (пом. 7), общий вид	

Допущения и предложения на листе

Основа листа: размеры сняты со скана обмерного плана KV design (см): часть подписей не читается, помещения выровнены по читаемым размерам; контрольный обмер не выполнен (К-1); высота потолка 2650 мм принята по отметкам обмера (Н = 2,50…2,66 м, ригель 2,28 м) — уточнить при обмере (К-2); толщины стен 300 / 120 мм приняты, межквартирная стена и колонны — по скану, не замерены (К-1); разрешённая мощность 15 кВт принята по типовым ТУ; при объединении двух квартир — переоформление ТУ (К-4); подрайон климата не задан — принят не северный (жилые от 2,5 м) (К-8).

См. лист открытых вопросов (лист 6, записи К-1, К-2, К-4, К-8).

Изм.	Кол.уч	Лист	№ док.	Подп.	Дата
Разраб.		Кырлан А.С.			04.11.26
Пров.					
ГИП					
Н. контр.					
Утв.					

ГД-2026-009-АИ

Квартира 103 м²

Общая площадь 100,72* м² · * размеры со скана, не замерены (реестр — л. 6, 7, К-1)

Дизайн-проект интерьера

Стадия	Лист	Листов
РП	4	120

Общие данные

М б/м

Кырлан Александр Сергеевич

выпуск 04.11.2026 № 20cec94f32 · стр. 4 из 130

Общие данные

Комплект ГД-2026-009-АИ · лист 4 общих данных (продолжение)

Состав дизайн-проекта

Раздел	Состав	Листы
Обложка	Дизайн-проект интерьера; Квартира 103 м²; автор проекта — Кырлан Александр Сергеевич	1 с.
Концепция	Стиль Мид-сенчури 65 % + Ар-деко 35 %: концепция интерьера, палитра и материалы (колерная карта — лист 57)	л. 18
Визуализации	25 изобр.: Вид сверху (3D): планировка с мебелью, текстилем и декором; Ванная, стена Б; Ванная, стена В; Ванная, стена Г; Ванная мастер, общий вид; Спальня 2, стена А; Спальня 2, стена Б; Спальня 2, стена Г; Спальня мастер, стена А; Спальня мастер, стена Б; Спальня мастер, стена В; Спальня мастер, стена Г; Коридор, стена Б; Прихожая-холл, стена А; Прихожая-холл, стена Б; Кухня, стена Б; Кухня, стена В; Гостиная-столовая, стена А; Гостиная-столовая, стена Б; Гостиная-столовая, стена В; Гостиная-столовая, стена Г; Кабинет-библиотека, стена А; Кабинет-библиотека, стена Б; Кабинет-библиотека, стена Г; Постирочная, общий вид	В1–В25
Рабочие чертежи	планы, развёртки, узлы (развёртки и узлы — листы 38–41, 79–82, 92, 94, 95, 98, 99, 108, 110, 113)	л. 1–120
Спецификации и ведомости	оборудование, изделия, отделка, электроточки	л. 17, 20–22, 26, 27, 42, 54–60, 64, 65, 114–118

Условные обозначения

- контрольный отрезок 1000 мм натуры: по нему проверяют печать 1:1
- отметка уровня, м: ±0,000 — чистый пол жилых помещений
- (А) марка развёртки: буква стены, стрелка — взгляд
- (О1) марка отделки по реестру отделки альбома
- выноска узла: над полкой — узел, под полкой — лист

Общие указания

1. Рабочие чертежи интерьера разработаны на основании задания на проектирование и обмерного плана (лист 14). Объект: Квартира 103 м²; автор проекта — Кырлан Александр Сергеевич; общая площадь 100,72 м², жилая 64,79 м², помещений 11.
2. Рабочие чертежи выполнены в соответствии с заданием на проектирование и нормативными документами, перечисленными в п. 4.
3. Открытые вопросы, принятые допущения и конфликты между разделами, не снятые к выпуску комплекта, сведены в таблицы на листах 6, 7. До ответа по пункту таблицы показанное на указанном там листе — допущение, а не утверждённое решение: комплект по этим листам предварительный.
4. Нормативные документы, на которые есть ссылки в листах комплекта: ГОСТ Р 21.101-2026; ГОСТ 21.501-2018; ГОСТ 2.302-68; ГОСТ 2.303-68; ГОСТ 2.304-81; ГОСТ 2.307-2011; СП 54.13330.2022; СП 71.13330.2017; СП 73.13330.2016; ПУЭ (7-е изд.), гл. 1.8, 7.1; ГОСТ Р 50571.7.701-2024; СанПиН 1.2.3685-21; ГОСТ 2.702; ГОСТ 2.755; ГОСТ 21.110-2013; ГОСТ 21.601; ГОСТ 13996-2019; ГОСТ 31173-2016; ГОСТ 31565-2012; ГОСТ 32414-2013; ГОСТ 32415-2013; ГОСТ Р 56387-2018; ГОСТ Р 56926; СП 29.13330.2011; СП 30.13330.2020; СП 51.13330.2011; СП 131.13330. Документы из ведомости ссылочных документов здесь не повторяются.
5. За отметку ±0,000 принят уровень чистого пола жилых помещений квартиры (относительная отметка; абсолютная — по проекту дома). Отметка чистого пола мокрых помещений — −0,015. Размеры — в миллиметрах, отметки — в метрах, площади — в м²; высоты установки Н от чистого пола своего помещения до оси изделия.
6. Несущие конструкции, общедомовые стояки, вентиляционные каналы и инженерные сети дома настоящим комплектом не изменяются. Работы, затрагивающие их (проём или штраба в несущей стене, перенос стояка, врезка в вентканал, расширение мокрой зоны), выполняются только по отдельному проекту, к которому прилагается техническое заключение о допустимости и безопасности работ, выданное автором проекта дома или организацией с допуском на обследование, и который согласован в установленном порядке (Жилищный кодекс РФ, ст. 25–29).
7. Трассы инженерных сетей на листах — принципиальные. Расчёты электрических нагрузок и токов КЗ, гидравлики, воздухообмена, освещённости и нагрузок на перекрытие выполняются в проектах ЭОМ, ВК, ОВ и КР организацией с допуском СРО; фактические трассы до закрытия отделкой фиксируются исполнительными схемами.
8. Стиль интерьера — Мид-сенчури 65 % + Ар-деко 35 %. Палитра проекта: основной 60 % — Farrow & Ball No. 291 «School House White — тёплый меловой белый», NCS S 0502-Y «Белый с лёгкой желтизной»; дополнительный 30 % — Farrow & Ball No. 298 «Bancha — оливковый середины века», Farrow & Ball No. 289 «Inchyra Blue — тёмный сине-серый», Farrow & Ball No. 255 «Tanner's Brown — тёмный шоколад»; акцент 10 % — NCS S 2050-Y20R «Горчичный», NCS S 3050-Y70R «Терракотовый / жжёный оранжевый», NCS S 5030-B10G «Тил», NCS S 5040-B90G «Изумрудный». Коды цвета — по веерам производителей; цвет утверждается по выкрасу на объекте при освещении проекта.
9. Площади поверхностей — по чистым граням стен до отделки: стены = периметр × высоту от чистого пола помещения до низа потолка минус проёмы (облицовка плиткой — до верха облицовки); плинтус = периметр минус дверные проёмы; пол и потолок — по площади помещения. Количество плиток — по раскладке. Способ один для всех листов комплекта (ведомость отделки, колерная карта, раскладка плитки, развёртки).
10. Марки: стены помещения на всех листах — А (верхняя по плану), Б (правая), В (нижняя), Г (левая); марка отделки О — одна на весь альбом; реестр марок отделки (с позициями колерной карты той же отделки) и марки позиций по видам — на листе 78.
11. Развёртки стен выполнены по всем помещениям для стен с электроточками, мебелью, декором и отделкой: санузлы и кухонный фронт — в М 1:25, остальные стены — в М 1:25; расположение развёрток и узлов — на листе 79, узлы — на листе 113.
12. Перечень скрытых работ, на которые составляются акты освидетельствования (форма по приказу Минстроя России № 344/пр): гидроизоляция пола и стен мокрых помещений (с тестом проливом); стяжка пола (толщина, прочность, влажность основания); скрытая электропроводка (за потолком и в штробах стен; условия штробления — в следующем пункте); трубопроводы водоснабжения и канализации до закрытия (опрессовка, уклоны); закладные и усиления под подвесные приборы, мебель и тяжёлый декор, рамы инсталляций; короба дверей скрытого монтажа до штукатурки; каркасы ГКЛ потолков, коробов и перегородок до обшивки.
13. Скрытая электропроводка: за потолком и в штробах стен. Штробы в стенах выполняются только после технического заключения о несущих конструкциях; до заключения несущие стены не определены, и все стены считаются несущими; объём штроб — в ведомости объёмов работ, строка «Штробы в стенах» (вертикальные спуски; объём не меньше фактического, горизонтальные трассы — по исполнительной схеме).
14. Критерии приёмки: допуски отделочных покрытий — по СП 71.13330.2017; испытания систем водоснабжения и канализации — по СП 73.13330.2016 до закрытия трасс; приёмо-сдаточные испытания электроустановки — по ПУЭ, гл. 1.8, с протоколом электролаборатории.
15. Осознанные отступления от ГОСТ Р 21.101-2026, принятые в комплекте: номер листа и число листов («Листов») указаны на каждом листе; на масштабных листах в основной надписи указан фактический масштаб и дан контрольный отрезок 1000 мм; развёртки стен выполнены в М 1:25 (ГОСТ 21.507-81 — 1:50…1:500) ради читаемости привязок; размерные числа и марки элементов (Д-1, ОК-1, О6) кеглем 2,5 мм, номера помещений — в кружке Ø 8 мм (канон — 3,5 мм и Ø 12 мм): так насыщенные листы А3 читаются без наложений надписей.
16. Графы «Пров.», «Н. контр.», «Утв.» основной надписи заполняются при согласовании комплекта с заказчиком; до согласования комплект подписывает автор проекта (графа «Разраб.»).

Допущения и предложения на листе

Основа листа: размеры сняты со скана обмерного плана KV design (см): часть подписей не читается, помещения выровнены по читаемым размерам; контрольный обмер не выполнен (К-1); высота потолка 2650 мм принята по отметкам обмера (Н = 2,50…2,66 м, ригель 2,28 м) — уточнить при обмере (К-2); толщины стен 300 / 120 мм приняты, межквартирная стена и колонны — по скану, не замерены (К-1); разрешённая мощность 15 кВт принята по типовым ТУ; при объединении двух квартир — переоформление ТУ (К-4); подрайон климата не задан — принят не северный (жилые от 2,5 м) (К-8).

См. лист открытых вопросов (лист 6, записи К-1, К-2, К-4, К-8).

Изм.	Кол.уч	Лист	№ док.	Подп.	Дата			
Разраб.		Кырлан А.С.			04.11.26	ГД-2026-009-АИ		
Пров.						Квартира 103 м²		
ГИП						Общая площадь 100,72* м² · * размеры со скана, не замерены (реестр — л. 6, 7, К-1)		
						Дизайн-проект интерьера	Стадия: РП	Лист: 5 / Листов: 120
Н. контр.						Общие данные	Кырлан Александр Сергеевич	
Утв.						М б/м		

выпуск 04.11.2026 № 20cec94f32 · стр. 5 из 130

Открытые вопросы, принятые допущения и конфликты. Лист 1 из 2

ПРЕДВАРИТЕЛЬНО · не для производства работ · открыто пунктов: 8 (реестр — л. 6, 7)

Сводка по реестрам координации (стартовое совещание 18.10.2026)

Комплект предварительный по пунктам этих таблиц. Пока по пункту нет ответа или решения, показанное на указанном листе — допущение проектировщика, а не утверждённое решение.
Сводка: открытых вопросов — 7 (из них ждут факта объекта — 4: контрольного обмера, обследования или документа); изменений в реестре — 1, из них без подписи — 1.
Пункты, ответ на которые лежит на объекте, а не за столом проектировщика (графа «Вид», строка «Ждёт»), собраны на листе «Задание на контрольный обмер и обследование» (листы 8–10): что и где замерить, с какой точностью и чем подтвердить. Пункты, ждущие решения человека, на объекте не закрываются.

Открытые вопросы и принятые допущения

№	Формулировка	Вид	Кто решает	Если решения нет	Лист, где это проявляется
К-1	Размеры сняты со скана обмерного плана KV design (в см): часть подписей не читается, помещения выровнены по читаемым размерам. До заказа мебели, дверей и материалов нужен контрольный обмер.	Отсутствует Ждёт: обмера	Архитектор-планировщик	размеры на листах — по плану заказчика, уточняются по месту; мебель на заказ и материалы по ним не заказывать	л. 14 — Обмерный план л. 19 — План расстановки мебели
К-2	Высота потолка принята 2650 мм по отметкам обмера (Н = 2,50…2,66 м); под ригелем 2,28 м — уточнить.	Отсутствует	Архитектор-планировщик	высоты на развёртках и потолки — от 2650 мм, уточнить при обмере	л. 14 — Обмерный план л. 45 — План потолков
К-4	Разрешённая мощность объединённой квартиры по ТУ неизвестна, принята 15 кВт; при объединении двух квартир ТУ переоформляются.	Отсутствует	Инженер-электрик	щит и группы рассчитаны на 15 кВт; при меньших ТУ пересчёт	л. 28 — Однолинейная схема щита л. 23 — План розеток и электровыводов
К-5	Объединение двух квартир в одну (проём в межквартирной стене между гостиной и коридором правой квартиры, вход — один из тамбура, второй вход закрывается; правая кухня — постирочная) — предложение проектировщика. Межквартирная стена, колонны и ригель — несущие или нет, неизвестно (на обмере отмечены «несущие колонны» и «ригель перекрытия»): нужны поэтажный план БТИ, техзаключение и согласование перепланировки (ЖК РФ ст. 25–29).	Отсутствует Ждёт: документа	Архитектор-планировщик	проём и перегородки — предложение, к строительству не выдаются; мокрые зоны и кухня оставлены на местах обмера	л. 14 — Обмерный план
К-6	Ванная мастер (пом. 11): стояки Ст К1-3 Ø110, Ст В1-3, Ст Т3-3 по данным стоят в углу стен В и Г (оси ≈ 90–240 мм от стены Г, 150–280 мм от стены В) — внутри габарита душевого поддона См1 800 × 800 у стены В, а душ со стеклоблочной перегородкой по плану сохраняется. Поддон на стояки не встанет, короба (зазор 50 мм) и люка 300 × 400 к арматуре нет. Положение стояков снято со скана обмера (К-1), отдельно не замерялось. Нужен контрольный обмер угла: оси стояков от двух стен, перегородка из стеклоблоков. Затем решить: (а) короб стояков в углу ≈ 310 × 350 с люком, поддон 800 × 800 сдвинуть вдоль стены В от короба, стеклоблочную перегородку разобрать и выложить заново по новому поддону; (б) поддон меньше, вне короба (по месту после обмера); (в) душ с трапом без поддона по обходу короба.	Спорно Ждёт: обмера, затем решения	Инженер ВК (вода, канализация)	душевую зону См1, поддон и перегородку не выполнять; выводы См1 и короб стояков — после обмера	л. 33 — План выводов сантехники л. 34 — Схема разводки водопровода и канализации л. 14 — Обмерный план
К-7	Унитаз подвесной Сн2 (пом. 6 «Ванная»), выпуск К1-2 Ø110: трасса до Ст К1-1 (1,91 м) идёт под дверным проёмом Д-5 — короб над полом там не поставить. Решить: (а) прибор ближе к стояку Ст К1-1 (без прохода под проёмом); (б) выпуск в полу с подъёмом пола помещения на 160 мм; (в) насосная установка (КНС) у прибора — по паспорту, требует согласования. Решение меняет санузел (высоты, раскладку плитки) — за автором с заказчиком.	Спорно Ждёт: решения	Инженер ВК (вода, канализация)	выпуск К1-2 и прибор Сн2 не выполнять до решения; остальное — по листам	л. 34 — Схема разводки водопровода и канализации л. 33 — План выводов сантехники
К-8	Климатический подрайон (СП 131.13330) не задан: принят не северный — жилые комнаты и кухня под потолком от 2,5 м (СП 54, п. 5.12); в IА, IБ, IГ, IД, IVА — от 2,7 м.	Отсутствует Ждёт: документа	Архитектор-планировщик	отметки потолков жилых — по 2,5 м; при северном подрайоне уровни ниже 2,7 м пересчитать до заказа каркаса	л. 45 — План потолков

Изменения проекта после выпуска листов (реестр изменений)

№	Дата	Лист	Было	Стало	Кто решил, подпись
ИЗ-1	30.10.2026	л. 28 — Однолинейная схема щита л. 23 — План розеток и электровыводов л. 51 — Раскладка плитки. Ванная. Развёртки стен л. 16 — План дверей л. 59 — Спецификация отделочных материалов л. 33 — План выводов сантехники	Фены Р8, Р33 и полотенцесушители В6, В7 сидели на гр. 13 «посудомоечная машина», стиральная машина Р50 — на гр. 12 «духовой шкаф»; групп 7 и 8 в щите не было. Два вывода печатались «ЭВ4» (духовой шкаф «ЭВ4» на кухне и вентилятор «В4» ванной). Окно 2 спальни мастер (offset 3500, 1300) выходило за стену Б (3830). Пол ванных и плинтус МДФ — без артикула. Стояки Ст К1-3/В1-3/Т3-3 без признака допущения.	Группы 7 (санузлы: фены, полотенцесушители, УЗО 10 мА) и 8 (стиральная машина постирочной) добавлены, точки переназначены. Выводы кухни — В1 (варочная), В2 (духовой шкаф), печать ЭВ1/ЭВ2 — марки на листах уникальны. Окно 2 — стена Б части 1, offset 100, знак «*» (К-1). Пол ванных — Marvel Travertine Sand Cross 60×60 AFUL, плинтус — Ultrawood Base 5340 83×15. Стояки ванной мастер — assumed, К-6; остаётся до обмера.	Не утверждено: подписи нет. решение исполнителя; на утверждение А. С. Кырлана

						ГД-2026-009-АИ	
						Квартира 103 м²	
Изм.	Кол.уч	Лист	№ док.	Подп.	Дата	Общая площадь 100,72* м² · * размеры со скана, не замерены (реестр — л. 6, 7, К-1)	
Разраб.		Кырлан А.С.			04.11.26	Дизайн-проект интерьера	Стадия: РП; Лист: 6; Листов: 120
Пров.							
ГИП						**Открытые вопросы, принятые допущения и конфликты. Лист 1 из 2** М б/м	**Кырлан Александр Сергеевич**
Н. контр.							
Утв.							

Открытые вопросы, принятые допущения и конфликты. Лист 2 из 2

Сводка по реестрам координации (стартовое совещание 18.10.2026)

ПРЕДВАРИТЕЛЬНО · не для производства работ · открыто пунктов: 8 (реестр — л. 6, 7)

Примечания

1. Номера листов — по ведомости рабочих чертежей комплекта (лист «Общие данные»).
2. Графа «Если решения нет» показывает состояние решения на листах; влияние на сроки и стоимость по пунктам не оценивалось.
3. Пункт, по которому принято решение, при следующем выпуске комплекта из таблиц исключается.

Допущения и предложения на листе

Основа листа: размеры сняты со скана обмерного плана KV design (см): часть подписей не читается, помещения выровнены по читаемым размерам; контрольный обмер не выполнен (К-1); высота потолка 2650 мм принята по отметкам обмера (Н = 2,50…2,66 м, ригель 2,28 м) — уточнить при обмере (К-2); толщины стен 300 / 120 мм приняты, межквартирная стена и колонны — по скану, не замерены (К-1); разрешённая мощность 15 кВт принята по типовым ТУ; при объединении двух квартир — переоформление ТУ (К-4); подрайон климата не задан — принят не северный (жилые от 2,5 м) (К-8).

См. лист открытых вопросов (лист 6, записи К-1, К-2, К-4, К-8).

Изм.	Кол.уч	Лист	№ док.	Подп.	Дата
Разраб.		Кырлан А.С.			04.11.26
Пров.					
ГИП					
Н. контр.					
Утв.					

ГД-2026-009-АИ

Квартира 103 м²

Общая площадь 100,72* м² · * размеры со скана, не замерены (реестр — л. 6, 7, К-1)

Дизайн-проект интерьера

Стадия	Лист	Листов
РП	7	120

Открытые вопросы, принятые допущения и конфликты. Лист 2 из 2

М б/м

Кырлан Александр Сергеевич

выпуск 04.11.2026 № 20cec94f32 · стр. 7 из 130

Задание на контрольный обмер и обследование. Лист 1 из 3

ПРЕДВАРИТЕЛЬНО · не для производства работ · открыто пунктов: 8 (реестр — л. 6, 7)

Что замерить, вскрыть и получить до заказа материалов и изделий

Задание собрано из открытых вопросов, ответ на которые лежит на объекте или в документах, а не за столом проектировщика. Пока факт не получен, размер, материал или положение на листах — допущение (знак «*»), а не замер.
Сводка: на объекте — 9 (до демонтажа — 7; после демонтажа — 2); документом и при закупке — 3; из допущений в данных и на листах — 10, из них без вопроса в реестре — 4. Закрываются вопросы: К-1, К-2, К-4–К-6, К-8 (6). Вопросы, ждущие решения человека, задание не закрывает — они решаются по реестру открытых вопросов.

Условия проведения

Порядок работ	Приёмы и точность	Кто присутствует	Если факт не совпал с проектом
1. До демонтажа — существующее состояние: контур, диагонали, высоты, проёмы, оси стояков, ниши и конструкции, которые видны. 2. После демонтажа, до черновых работ — то, что закрывали отделка и короба: основание стен, фактические толщины, углы, узлы. 3. Документы и данные закупки — не на объекте: к сроку из последней таблицы, от них зависят привязки и заказ. Что заказывается по размеру из задания, до закрытия пункта не заказывают: сроки изготовления — по графику закупок прораба.	Обход по часовой стрелке от входа: стены, проёмы, потолок, коммуникации (стояки, щиток, вентканалы), особенности (ниши, короба, выступы). Размеры записывают в мм; сумма участков равна общему размеру, при цепочке длиннее трёх участков ставят проверочный (общий) размер. Диагонали каждого помещения; если две диагонали различаются на 5 мм и больше, разницу подписывают на плане. Потолок — в нескольких точках: центр, углы, у проёмов. Проём — ширина, высота, глубина откоса, привязка к ближайшим углам, высота подоконника. Допустимая погрешность прибора — 2–3 мм на метр; размеры округляют кратно 5 мм; два контрольных промера одного размера не должны расходиться более чем на 2 %. Допуск по пункту — в графе «Точность». План БТИ обмер не заменяет.	Прораб (отвечает за проведение) — назначает день и порядок обхода, открывает объект и освобождает помещения, ведёт это задание и реестр изменений. Архитектор — выполняет обмер, составляет акт контрольного обмера и подписывает результаты по размерам и конструкциям. Владельцы вопросов присутствуют при пунктах своего раздела или принимают результат до заказа: Инженер ВК (вода, канализация) — К-6; Инженер-электрик — К-4; позиции О-1; Инженер ОВ — позиции О-2; Отделочник — позиции О-8, О-9. Заказчик или его представитель — передаёт документы (план БТИ, проект дома, технические условия, паспорта), подписывает акт. Проектных решений на обмере не принимают: обмер даёт факт, решения — по реестру открытых вопросов (листы 6–7).	1. В пределах допуска пункта — принимается измеренное значение, лист перевыпускается, знак «*» снимается. 2. Больше допуска или контрольные промеры расходятся более чем на 2 % — промер повторяют; не подтвердилось — запись в реестр изменений (дата, лист, было, стало, кто решил, подпись), работы в этом месте не начинают. 3. Затронуты несущая стена, стояк, вентканал или мокрая зона — сразу владельцу раздела и ГИПу (главному инженеру проекта); между разделами не больше двух кругов, затем решает ГИП. 4. На объекте устно ничего не согласуется: каждое решение — записью в реестр с подписью.

Этап 1. До демонтажа

№	Где	Способ	Что сделать	Кто выполняет	Точность	Что пересчитается в альбоме	Чем подтверждается	Закрывает вопросы реестра
О-1	Вход в квартиру или лестничная клетка; место щита на плане	Обмер	Существующий щиток и счётчик электроэнергии: место и габарит ниши, состояние ввода, марка и сечение вводного кабеля, наличие вводного автомата и УЗО, пломбы.	Архитектор	±5 мм	Ниша и место щита на листах; вводной кабель и аппараты на однолинейной схеме; расстояния до первых групп. Листы: л. 28 — Однолинейная схема щита	акт контрольного обмера; фото с рулеткой и привязкой к стене или углу	Вопроса в реестре нет: Альбом принимает щит и ввод без осмотра. Результат принимает: Инженер-электрик
О-2	Кабинет-библиотека (пом. 1), Гостиная-столовая (пом. 3), Кухня (пом. 5), Спальня 2 (пом. 8), Спальня мастер (пом. 10); у окон	Обмер	Положение стояков отопления (подающий и обратный) от граней стен, диаметры, наличие запорной арматуры; существующие радиаторы: число секций, межосевое расстояние, подводки. В данных стояков отопления нет — лист отопления выводит их условно у откоса окна, радиаторы — «принципиально, по расчёту».	Архитектор	±5 мм	План отопления: места стояков и подводок, привязки радиаторов; подбор радиаторов по теплотехническому расчёту; радиаторы и узлы подключения в ВОР и спецификации. Листы: л. 32 — План отопления	акт контрольного обмера; фото с рулеткой и привязкой к стене или углу	Вопроса в реестре нет: Альбом принимает положение стояков и радиаторов отопления без обмера. Результат принимает: Инженер ОВ
О-3	все помещения	Обмер	Контрольный обмер всех помещений: стороны, диагонали, проёмы, высота потолка.	исполнитель	±5 мм; диагонали — разница от 5 мм подписывается	обмерный и монтажный планы, развёртки, мебель на заказ Листы: л. 14 — Обмерный план л. 19 — План расстановки мебели	акт контрольного обмера	К-1 Результат принимает: Архитектор
О-4	Все помещения квартиры	Обмер	Высота потолка в каждом помещении в нескольких точках: центр, углы, у проёмов.	Архитектор	±5 мм	Вертикальные размеры альбома: развёртки, шкафы, плитка, объёмы работ. Листы: л. 2–5 — Общие данные	акт контрольного обмера	К-2 Результат принимает: Архитектор
О-5	По месту	Обмер	Подтвердить на объекте принятое: подрайон климата не задан — принят не северный (жилые от 2,5 м)	Архитектор	±5 мм	Листы, где используется принятая величина. Листы: л. 2–5 — Общие данные	акт контрольного обмера	К-8 Результат принимает: Архитектор

Допущения и предложения на листе
Основа листа: размеры сняты со скана обмерного плана KV design (см): часть подписей не читается, помещения выровнены по читаемым размерам; контрольный обмер не выполнен (К-1); высота потолка 2650 мм принята по отметкам обмера (Н = 2,50…2,66 м, ригель 2,28 м) — уточнить при обмере (К-2); толщины стен 300 / 120 мм приняты, межквартирная стена и колонны — по скану, не замерены (К-1); разрешённая мощность 15 кВт принята по типовым ТУ; при объединении двух квартир — переоформление ТУ (К-4); подрайон климата не задан — принят не северный (жилые от 2,5 м) (К-8).
См. лист открытых вопросов (лист 6, записи К-1, К-2, К-4, К-8).

Изм.	Кол.уч	Лист	№ док.	Подп.	Дата
Разраб.		Кырлан А.С.			04.11.26
Пров.					
ГИП					
Н. контр.					
Утв.					

ГД-2026-009-АИ

Квартира 103 м²

Общая площадь 100,72* м² · * размеры со скана, не замерены (реестр — л. 6, 7, К-1)

Дизайн-проект интерьера

Стадия	Лист	Листов
РП	8	120

Задание на контрольный обмер и обследование.
Лист 1 из 3
М б/м

Кырлан Александр Сергеевич

выпуск 04.11.2026 № 20cec94f32 · стр. 8 из 130

Задание на контрольный обмер и обследование. Лист 2 из 3

Что замерить, вскрыть и получить до заказа материалов и изделий

Этап 1. До демонтажа (продолжение)

№	Где	Способ	Что сделать	Кто выполняет	Точность	Что пересчитается в альбоме	Чем подтверждается	Закрывает вопросы реестра
О-6	Спальня мастер (пом. 10): окно пом. 10, стена Б	Обмер	Окно пом. 10, стена Б: положение (привязки к ближайшим углам), ширина, высота, высота подоконника, глубина откоса. Принято в проекте: Окно 1300 при offset 3500 на стене Б основной части (длина 3830) выходило за стену на 970 мм. Отнесено к стене Б части 1 (у 6300…7800): offset 100 положение со скана, не замерено..	Архитектор	±5 мм	Проёмы на обмерном плане и в ведомости проёмов; откосы и оконные работы в ВОР; привязки мебели и выводов к проёмам. Листы: л. 14 — Обмерный план л. 17 — Ведомость заполнения проёмов	акт контрольного обмера; фото с рулеткой и привязкой к стене или углу	К-1 Результат принимает: Архитектор
О-7	Ванная мастер (пом. 11): Ст К1-3*, Ст В1-3, Ст Т3-3*; наличие стояка ГВС, арматуры и счётчиков — по всей квартире	Обмер	Положение стояков Ст К1-3*, Ст В1-3*, Ст Т3-3*: привязка осей от граней стен, диаметры, размеры короба и люков. Стояк горячей воды Т3 в данных не задан, на листах ВК принят рядом с стояком холодной воды: выяснить, есть ли он в доме, и где. Отключающая арматура и счётчики воды на вводах: положение, тип, пломбы управляющей компании. Сверить до разметки выводов.	Архитектор	±5 мм	Привязки выводов воды и канализации на планах выводов и разводки; расстояние розеток до стояка; места люков 300 × 400 мм; трассы Т3 и полотенцесушители (водяной или электрический); узлы ввода в спецификации ВК (краны, фильтры, счётчики). короб и люк стояков, поддон См1, выводы душа, раскладка плитки ванной мастер Листы: л. 33 — План выводов сантехники л. 34 — Схема разводки водопровода и канализации л. 14 — Обмерный план	акт контрольного обмера; фото с рулеткой и привязкой к стене или углу	К-6 Результат принимает: Инженер ВК (вода, канализация)

Этап 2. После демонтажа, до черновых работ

№	Где	Способ	Что сделать	Кто выполняет	Точность	Что пересчитается в альбоме	Чем подтверждается	Закрывает вопросы реестра
О-8	Кабинет-библиотека (пом. 1), Кладовая (пом. 2), Гостиная-столовая (пом. 3), Прихожая-холл (пом. 4), Кухня (пом. 5), Ванная (пом. 6), Постирочная (пом. 7), Спальня 2 (пом. 8), Коридор (пом. 9), Спальня мастер (пом. 10), Ванная мастер (пом. 11)	Обмер	Нивелировка плиты перекрытия и существующего пола после демонтажа покрытий: отметки в углах и по сетке, перепады по помещению, уклоны, отметки порогов (чистый пол в мокрых зонах принят -15 мм, 0 мм). Принятая толщина стяжки 33 мм, 47 мм, 49 мм, 50 мм и отметка чистого пола — расчётные, не от замера плиты.	Архитектор	±5 мм по отметке; ровность просвет под 2-метровой рейкой, горизонталь против 0,2 % длины помещения	Толщина стяжки и отметка чистого пола; уклоны к трапам и пороги; выпуски К1 относительно чистого пола (план разводки); объёмы стяжки и смеси в ВОР и спецификации. Листы: л. 49, 53 — План полов л. 34 — Схема разводки водопровода и канализации	акт контрольного обмера	Вопроса в реестре нет: Альбом принимает отметки плиты и толщину пирога пола без нивелировки. Результат принимает: Отделочник
О-9	Кабинет-библиотека (пом. 1), Кладовая (пом. 2), Гостиная-столовая (пом. 3), Прихожая-холл (пом. 4), Кухня (пом. 5), Ванная (пом. 6), Постирочная (пом. 7), Спальня 2 (пом. 8), Коридор (пом. 9), Спальня мастер (пом. 10), Ванная мастер (пом. 11)	Обмер	Вертикаль и плоскостность стен: отклонение от вертикали по высоте стены (отвес или лазерный уровень), просвет под правилом 2 м, кривизна углов. Нужно там, где от стены зависит изделие: облицовка плиткой (пом. 6, 11), штукатурка и окраска (пом. 1, 2, 3, 4, 5, 6, 7, 8, 9, 10, 11), встроенная мебель и кухня (пом. 4, 5, 8, 10).	Архитектор	до 1 мм на 2 м (правило и клиновой щуп); вертикаль — мм на высоту стены, отклонения подписываются на плане	Толщина штукатурки и расход смеси в ВОР и спецификации; раскладка плитки (подрезка у стен); зазоры и крепление встроенной мебели и кухни. Листы: л. 49–52 — Раскладка плитки л. 54–56 — Ведомость отделки помещений	акт контрольного обмера	Вопроса в реестре нет: Альбом принимает стены ровными и вертикальными без замера. Результат принимает: Отделочник

Допущения и предложения на листе

Основа листа: размеры сняты со скана обмерного плана KV design (см): часть подписей не читается, помещения выровнены по читаемым размерам; контрольный обмер не выполнен (К-1); высота потолка 2650 мм принята по отметкам обмера (Н = 2,50…2,66 м, ригель 2,28 м) — уточнить при обмере (К-2); толщины стен 300 / 120 мм приняты, межквартирная стена и колонны — по скану, не замерены (К-1); разрешённая мощность 15 кВт принята по типовым ТУ; при объединении двух квартир — переоформление ТУ (К-4); подрайон климата не задан — принят не северный (жилые от 2,5 м) (К-8).

Знак «*» — принято, не замерено и не подтверждено (замерить на объекте): К-6: Ст К1-3, Ст В1-3, Ст Т3-3 — положение снято со скана обмера, отдельно не замерялось; ось внутри габарита поддона См1 — обмер угла по К-6.

См. лист открытых вопросов (лист 6, записи К-1, К-2, К-4, К-6, К-8).

Изм.	Кол.уч	Лист	№ док.	Подп.	Дата
Разраб.		Кырлан А.С.			04.11.26
Пров.					
ГИП					
Н. контр.					
Утв.					

ГД-2026-009-АИ

Квартира 103 м²

Общая площадь 100,72* м² · * размеры со скана, не замерены (реестр — л. 6, 7, К-1)

Дизайн-проект интерьера

Стадия	Лист	Листов
РП	9	120

Задание на контрольный обмер и обследование.
Лист 2 из 3
М б/м

Кырлан Александр Сергеевич

выпуск 04.11.2026 № 20cec94f32 · стр. 9 из 130

Задание на контрольный обмер и обследование. Лист 3 из 3

ПРЕДВАРИТЕЛЬНО · не для производства работ · открыто пунктов: 8 (реестр — л. 6, 7)

Что замерить, вскрыть и получить до заказа материалов и изделий

Документы и данные закупки (не на объекте)

№	У кого, откуда	Способ	Что получить	К какому сроку	Что пересчитается в альбоме	Чем подтверждается	Закрывает вопросы реестра
О-10	Заказчик; организация, выдавшая технические условия	Документ	Технические условия на присоединение: разрешённая мощность.	До утверждения однолинейной схемы щита	Однолинейная схема щита: вводной аппарат и группы. Листы: л. 2–5 — Общие данные	копия документа	К-4 Результат принимает: Инженер-электрик
О-11	вся квартира	Документ	Поэтажный план БТИ и техническое заключение о несущих стенах.	до демонтажа и возведения перегородок	монтажный план, проёмы, развёртки Листы: л. 14 — Обмерный план	копия документа	К-5 Результат принимает: Архитектор
О-12	адрес объекта, СП 131.13330	Документ	Климатический подрайон по СП 131.13330 (по адресу объекта)	до заказа каркаса потолков	план потолков, разрезы, ведомость объёмов Листы: л. 45 — План потолков	копия документа	К-8 Результат принимает: Архитектор

Примечания

1. Подтверждение: акт контрольного обмера (дата, кто присутствовал, прибор, перечень промеров с результатами, подписи присутствующих); к акту — фото вскрытий и узлов и техническое заключение организации, выполнившей обследование.
2. Номера листов — по ведомости рабочих чертежей комплекта (лист «Общие данные»).
3. Пункт исключается из задания при следующем выпуске, когда акт подписан, значение внесено в проект и листы перевыпущены; знак «*» у величины снимается только замером.

Допущения и предложения на листе

Основа листа: размеры сняты со скана обмерного плана KV design (см): часть подписей не читается, помещения выровнены по читаемым размерам; контрольный обмер не выполнен (К-1); высота потолка 2650 мм принята по отметкам обмера (Н = 2,50…2,66 м, ригель 2,28 м) — уточнить при обмере (К-2); толщины стен 300 / 120 мм приняты, межквартирная стена и колонны — по скану, не замерены (К-1); разрешённая мощность 15 кВт принята по типовым ТУ; при объединении двух квартир — переоформление ТУ (К-4); подрайон климата не задан — принят не северный (жилые от 2,5 м) (К-8).

См. лист открытых вопросов (лист 6, записи К-1, К-2, К-4, К-8).

Изм.	Кол.уч	Лист	№ док.	Подп.	Дата
Разраб.		Кырлан А.С.			04.11.26
Пров.					
ГИП					
Н. контр.					
Утв.					

ГД-2026-009-АИ

Квартира 103 м²

Общая площадь 100,72* м² · * размеры со скана, не замерены (реестр — л. 6, 7, К-1)

Дизайн-проект интерьера

Стадия	Лист	Листов
РП	10	120

Задание на контрольный обмер и обследование.
Лист 3 из 3
М б/м

Кырлан Александр Сергеевич

График закупок и работ. Лист 1 из 3

ПРЕДВАРИТЕЛЬНО · не для производства работ · открыто пунктов: 8 (реестр — л. 6, 7)

Что заказывать и когда не раньше чего: относительный порядок без дат; срок поставки — из данных или «не задан» с записью реестра

Лист не содержит дат: контрольного обмера, подписанных решений автора и договоров ещё нет, и любая дата была бы выдумана. Вместо календаря — порядок и условия: замер → решение и выбор изделия → заказ → срок поставки → работа, которую позиция блокирует.
Срок поставки печатается как срок, только если он задан в данных позиции. Нет — «срок поставки не задан» и ссылка на вопрос реестра о сроках; типовой диапазон практики стоит рядом как ориентир и заказывать по нему нельзя. Номера З-N и Р-N — строки этого листа, К-N — записи реестра открытых вопросов, О-N — позиции задания на контрольный обмер.

Закупки: что заказывается, от чего зависит заказ и какую работу блокирует

№	Позиция и где	1. Замер до заказа	2. Решение, выбор изделия, паспорт	3. Условие заказа	4. Срок поставки	5. Блокирует работу	Закрывает вопросы реестра
З-1	Двери скрытого монтажа с коробом под покраску в существующих проёмах: Д-2, Д-3, Д-4, Д-5, Д-6, Д-7, Д-8, Д-9 — 8 шт. пом. 1, 2, 5, 6, 7, 8, 10, 11	О-6: обмер: Спальня мастер (пом. 10): окно пом. 10, стена Б (К-1) О-3: обмер: все помещения (К-1); до заказа мебели и дверей		После 1 и 2 и после получения срока у поставщика (вопроса о сроках нет); дата заказа — когда срок известен, не позднее чем за срок до начала Р-5.	срок поставки не задан (записи реестра нет) Ориентир практики (не срок поставщика): ≈ 30 дн.	Р-5 «штукатурка»: короб ставят до штукатурки (коробку ставят на черновой стадии; полотно навешивают после чистовой отделки стен)	К-1
З-2	Кухонный гарнитур по проекту кухни: модули Кх1, Кх2, Кх3, Кх4, Кх7, Кх5, Кх8** пом. 5			После 1 и 2 и после получения срока у поставщика (вопроса о сроках нет); дата заказа — когда срок известен, не позднее чем за срок до начала Р-15.	срок поставки не задан (записи реестра нет) Ориентир практики (не срок поставщика): 4–8 нед. от замера	Р-15 «кухня и мебель»: замер кухни — по готовым стенам после штукатурки или плитки, до чистового пола; производство идёт параллельно со стяжкой и отделкой	
З-3	Встраиваемая техника кухни: Кх2 посудомоечная машина, Кх4 oven, Кх5 холодильник, Кх8** вытяжка пом. 5			После 1 и 2 и после получения срока у поставщика (вопроса о сроках нет); дата заказа — когда срок известен, не позднее чем за срок до начала Р-15.	срок поставки не задан (записи реестра нет)	Р-15 «кухня и мебель»: паспорта и монтажные схемы — до изготовления модулей кухни: нишу и вентзазоры задаёт модель, а не типовая схема 60 см	
З-4	Стиральная машина: Пм1 (вертикальная загрузка 400 × 600 мм — условие закупки) пом. 7			После 1 и 2 и после получения срока у поставщика (вопроса о сроках нет); дата заказа — когда срок известен, не позднее чем за срок до начала Р-4.	срок поставки не задан (записи реестра нет)	Р-4 «черновая сантехника»: габарит и подводка — до закрытия люка и разводки	
З-5	Сантехнические приборы и инсталляции: Сн1, Сн2, Сн3, См1, См2, См3 пом. 6, 11	О-7: обмер: Ванная мастер (пом. 11): Ст К1-3, Ст В1-3*, Ст Т3-3*; наличие стояка ГВС, арматуры и счётчиков — по всей квартире (К-6) О-2: обмер: Кабинет-библиотека (пом. 1), Гостиная-столовая (пом. 3), Кухня (пом. 5), Спальня 2 (пом. 8), Спальня мастер (пом. 10); у окон		После 1 и 2 и после получения срока у поставщика (вопроса о сроках нет); дата заказа — когда срок известен, не позднее чем за срок до начала Р-4.	срок поставки не задан (записи реестра нет)	Р-4 «черновая сантехника»: инсталляцию ставят до обшивки ГКЛВ и до гидроизоляции стены	К-6
З-6	Керамогранит и плитка: 2 поз. по артикулу и формату, 51,07 м² по раскладке пом. 4, 6, 11	О-8: обмер: Кабинет-библиотека (пом. 1), Кладовая (пом. 2), Гостиная-столовая (пом. 3), Прихожая-холл (пом. 4), Кухня (пом. 5), Ванная (пом. 6), Постирочная (пом. 7), Спальня 2 (пом. 8), Коридор (пом. 9), Спальня мастер (пом. 10), Ванная мастер (пом. 11) О-9: обмер: Кабинет-библиотека (пом. 1), Кладовая (пом. 2), Гостиная-столовая (пом. 3), Прихожая-холл (пом. 4), Кухня (пом. 5), Ванная (пом. 6), Постирочная (пом. 7), Спальня 2 (пом. 8), Коридор (пом. 9), Спальня мастер (пом. 10), Ванная мастер (пом. 11)		После 1 и 2 и после получения срока у поставщика (вопроса о сроках нет); дата заказа — когда срок известен, не позднее чем за срок до начала Р-9.	срок поставки не задан (записи реестра нет)	Р-9 «плитка»: калибр партии измеряют до раскладки, раскладку пересчитывают до заказа	

Допущения и предложения на листе

Основа листа: размеры сняты со скана обмерного плана KV design (см): часть подписей не читается, помещения выровнены по читаемым размерам; контрольный обмер не выполнен (К-1); высота потолка 2650 мм принята по отметкам обмера (Н = 2,50…2,66 м, ригель 2,28 м) — уточнить при обмере (К-2); толщины стен 300 / 120 мм приняты, межквартирная стена и колонны — по скану, не замерены (К-1); разрешённая мощность 15 кВт принята по типовым ТУ; при объединении двух квартир — переоформление ТУ (К-4); подрайон климата не задан — принят не северный (жилые от 2,5 м) (К-8).
Знак «*» — принято, не замерено и не подтверждено (замерить на объекте): К-6: Ст В1-3, Ст Т3-3 — положение снято со скана обмера, отдельно не замерялось; ось внутри габарита поддона См1 — обмер угла по К-6.
Знак «**» — предложение проектировщика, заказчиком не утверждено (согласовать с заказчиком): Кх8 — над индукционной панелью Кх4 нужна вытяжка: в составе кухни её не было, розетка вытяжки образца висела без потребителя.
См. лист открытых вопросов (лист 6, записи К-1, К-2, К-4, К-6, К-8).

Изм.	Кол.уч	Лист	№ док.	Подп.	Дата				
Разраб.		Кырлан А.С.			04.11.26	ГД-2026-009-АИ			
Пров.						Квартира 103 м² Общая площадь 100,72* м² · * размеры со скана, не замерены (реестр — л. 6, 7, К-1)			
ГИП						Дизайн-проект интерьера	Стадия: РП	Лист: 11	Листов: 120
Н. контр.						**График закупок и работ. Лист 1 из 3** М б/м	**Кырлан Александр Сергеевич**		
Утв.									

выпуск 04.11.2026 № 20cec94f32 · стр. 11 из 130

График закупок и работ. Лист 2 из 3

Что заказывать и когда не раньше чего: относительный порядок без дат; срок поставки — из данных или «не задан» с записью реестра

Закупки: что заказывается, от чего зависит заказ и какую работу блокирует (продолжение)

№	Позиция и где	1. Замер до заказа	2. Решение, выбор изделия, паспорт	3. Условие заказа	4. Срок поставки	5. Блокирует работу	Закрывает вопросы реестра
З-7	Покрытие пола (доска) и плинтус: пом. 1, 2, 3, 5, 7, 8, 9, 10 пом. 1, 2, 3, 5, 7, 8, 9, 10	О-8: обмер: Кабинет-библиотека (пом. 1), Кладовая (пом. 2), Гостиная-столовая (пом. 3), Прихожая-холл (пом. 4), Кухня (пом. 5), Ванная (пом. 6), Постирочная (пом. 7), Спальня 2 (пом. 8), Коридор (пом. 9), Спальня мастер (пом. 10), Ванная мастер (пом. 11)		После 1 и 2 и после получения срока у поставщика (вопроса о сроках нет); дата заказа — когда срок известен, не позднее чем за срок до начала Р-12.	срок поставки не задан (записи реестра нет)	Р-12 «чистовые полы»: артикул и партия — до заказа; доску привозят к чистовым полам	
З-8	Встроенная мебель по замеру цеха: П1, С2, М4 пом. 4, 8, 10	О-3: обмер: все помещения (К-1); до заказа мебели и дверей		После 1 и 2 и после получения срока у поставщика (вопроса о сроках нет); дата заказа — когда срок известен, не позднее чем за срок до начала Р-15.	срок поставки не задан (записи реестра нет) Ориентир практики (не срок поставщика): 4–8 нед. от замера	Р-15 «кухня и мебель»: цех замеряет по готовым стенам; производство 4–8 недель идёт параллельно с отделкой	К-1

Работы: порядок и что не даёт начать

№	Работа (стадия технологической последовательности)	После	Что должно быть к началу: условия и закупки	Не начинать, пока открыто в реестре
Р-1	Демонтаж покрытий, отделки стен и потолков, дверных блоков и приборов; конструкции, стены и перегородки не трогать до технического заключения (стадия 1)		до начала: запрошены документы на дом и БТИ; контрольный обмер до демонтажа (что видно) сделан	
Р-2	Контрольный обмер на голых стенах и обследование (задание — лист «Задание на контрольный обмер») (стадия 2)	Р-1	после снятия отделки: видны стояки, каналы, щиток, толщины стен; до заказа всего, что делают по размеру	
Р-3	Черновая электрика: штробы, короба, гофра, подрозетники, щит (стадия 4)	Р-2	до начала: план электрики с высотами утверждён; штробы в стенах — только после технического заключения; мебель расставлена	К-4: Разрешённая мощность объединённой квартиры по ТУ неизвестна, принята 15 кВт; при объединении двух квартир ТУ переоформляются.
Р-4	Черновая сантехника и вентиляция: разводка, выводы, инсталляции, короба стояков (стадия 5)	Р-2	до начала: положение стояков замерено; модели инсталляций и машины выбраны (габариты рамы, подводка); инсталляцию ставят до обшивки ГКЛВ и до гидроизоляции Закупки к началу: З-4 (стиральная машина), З-5 (сантехника)	К-6: Ванная мастер (пом.
Р-5	Коробки скрытых дверей, затем штукатурка стен и откосов (стадия 6)	Р-2, Р-3, Р-4	до начала: электрика и сантехника смонтированы, штробы заделаны; коробки скрытых дверей установлены до штукатурки (поэтому заказ дверей — раньше работы) Закупки к началу: З-1 (двери скрытого монтажа)	К-1: Размеры сняты со скана обмерного плана KV design (в см): часть подписей не читается, помещения выровнены по читаемым размерам.
Р-6	Стяжка пола и тёплый пол (стадия 7)	Р-5	до начала: штукатурка сделана; трубы под стяжкой приняты; нивелировка плиты выполнена	
Р-7	Гидроизоляция санузлов и тест проливом (стадия 8)	Р-6	до начала: стяжка набрала прочность и сухая по инструкции гидроизоляции; выводы стоят на проектных отметках	
Р-8	ГКЛ: короба инсталляции и стояков, ниши, потолки (стадия 9)	Р-3, Р-4	до начала: черновые сети в зоне коробов приняты; закладные под тяжёлое и карнизы стоят; светильники выбраны (вырезы)	
Р-9	Плитка и керамогранит: стены, затем пол; фартук (стадия 10)	Р-6, Р-7, Р-8	до начала: гидроизоляция принята; плитка выбрана, калибр партии измерен, раскладка пересчитана и подписана Закупки к началу: З-6 (плитка)	
Р-10	Шпаклёвка стен и потолков под окраску (стадия 11)	Р-5, Р-8, Р-9	до начала: плитка готова (грязные работы закончены); штукатурка и ГКЛ сухие	

Допущения и предложения на листе

Основа листа: размеры сняты со скана обмерного плана KV design (см): часть подписей не читается, помещения выровнены по читаемым размерам; контрольный обмер не выполнен (К-1); высота потолка 2650 мм принята по отметкам обмера (Н = 2,50…2,66 м, ригель 2,28 м) — уточнить при обмере (К-2); толщины стен 300 / 120 мм приняты, межквартирная стена и колонны — по скану, не замерены (К-1); разрешённая мощность 15 кВт принята по типовым ТУ; при объединении двух квартир — переоформление ТУ (К-4); подрайон климата не задан — принят не северный (жилые от 2,5 м) (К-8).

См. лист открытых вопросов (лист 6, записи К-1, К-2, К-4, К-8).

Изм.	Кол.уч	Лист	№ док.	Подп.	Дата
Разраб.		Кырлан А.С.			04.11.26
Пров.					
ГИП					
Н. контр.					
Утв.					

ГД-2026-009-АИ

Квартира 103 м²

Общая площадь 100,72* м² · * размеры со скана, не замерены (реестр — л. 6, 7, К-1)

Дизайн-проект интерьера

Стадия	Лист	Листов
РП	12	120

График закупок и работ. Лист 2 из 3

М б/м

Кырлан Александр Сергеевич

выпуск 04.11.2026 № 20cec94f32 · стр. 12 из 130

График закупок и работ. Лист 3 из 3

ПРЕДВАРИТЕЛЬНО · не для производства работ · открыто пунктов: 8 (реестр — л. 6, 7)

Что заказывать и когда не раньше чего: относительный порядок без дат; срок поставки — из данных или «не задан» с записью реестра

Работы: порядок и что не даёт начать (продолжение)

№	Работа (стадия технологической последовательности)	После	Что должно быть к началу: условия и закупки	Не начинать, пока открыто в реестре
Р-11	Окраска стен, потолков, откосов (стадия 13)	Р-10	до начала: шпаклёвка отшлифована и огрунтована; выкрасы утверждены, колеровка одной партией	
Р-12	Чистовые полы: инженерная доска (стадия 14)	Р-9, Р-11	до начала: влажность основания в норме, мокрые работы закончены; доска выбрана и привезена Закупки к началу: З-7 (доска и плинтус)	
Р-13	Полотна межкомнатных дверей, плинтусы, пороги (стадия 15)	Р-11, Р-12	до начала: чистовой пол уложен; полотна скрытых дверей — после чистовой отделки стен	
Р-14	Чистовая электрика и сантехника: механизмы, светильники, смесители, приборы (стадия 16)	Р-11, Р-13	до начала: отделка готова; механизмы, светильники и приборы выбраны и привезены	
Р-15	Кухня, встроенная и корпусная мебель, бытовая техника (стадия 17)	Р-13, Р-14	до начала: чистовая сантехника и электрика подведены к местам мебели; замер кухни снят по готовым стенам (после штукатурки или плитки, до чистового пола) Закупки к началу: З-2 (кухонный гарнитур), З-3 (техника кухни), З-8 (мебель по замеру)	К-1: Размеры сняты со скана обмерного плана KV design (в см): часть подписей не читается, помещения выровнены по читаемым размерам.
Р-16	Сдача: осмотр по чек-листу, дефектная ведомость, устранение замечаний (стадия 18)	Р-14, Р-15	до начала: всё смонтировано; акты скрытых работ подписаны	

Примечания

1. Порядок работ — стадии технологической последовательности из 16 позиций, присутствующих в этом проекте (по строкам ведомости объёмов); остальные стадии таблицы knowledge/remont-tehnologiya.md в проекте не встречаются. Длительности работ не печатаются: их нет ни в данных, ни в нормах для этого объекта.
2. Типовые сроки — ориентир практики, не срок поставщика: скрытые двери — короб около 10 дн., полотно под покраску до 3 нед., шпон 4–5 нед., в среднем около 30 дн. (knowledge/workers/foreman.md, п. 2.4 (profil-doors)); кухня и корпусная мебель — 4–8 недель от замера (knowledge/remont-tehnologiya.md, разд. 2; knowledge/workers/foreman.md, п. 2.4). Заказ по ориентиру не назначается: срок получают у поставщика (вопрос реестра), после чего заказ планируют «не позднее чем за срок до начала работы».
3. Условия заказа берутся из реестра открытых вопросов и задания на контрольный обмер: позиция заказывается, когда закрыты замер (графа 1) и решение (графа 2). Закрывать их может только факт или решение автора с подписью; снять строку с листа можно только закрыв запись реестра.
4. Заказ по размеру до контрольного обмера не делают: двери, кухня и встроенная мебель зависят от обмера (К-11, К-13); скрытые двери, кроме того, зависят от решения по нише санузла 2 (проём Д-5 в перегородке П-1).
5. Номера листов — по ведомости рабочих чертежей комплекта (лист «Общие данные»).

Допущения и предложения на листе

Основа листа: размеры сняты со скана обмерного плана KV design (см): часть подписей не читается, помещения выровнены по читаемым размерам; контрольный обмер не выполнен (К-1); высота потолка 2650 мм принята по отметкам обмера (Н = 2,50…2,66 м, ригель 2,28 м) — уточнить при обмере (К-2); толщины стен 300 / 120 мм приняты, межквартирная стена и колонны — по скану, не замерены (К-1); разрешённая мощность 15 кВт принята по типовым ТУ; при объединении двух квартир — переоформление ТУ (К-4); подрайон климата не задан — принят не северный (жилые от 2,5 м) (К-8).
См. лист открытых вопросов (лист 6, записи К-1, К-2, К-4, К-8).

Изм.	Кол.уч	Лист	№ док.	Подп.	Дата
Разраб.		Кырлан А.С.			04.11.26
Пров.					
ГИП					
Н. контр.					
Утв.					

ГД-2026-009-АИ

Квартира 103 м²

Общая площадь 100,72* м² · * размеры со скана, не замерены (реестр — л. 6, 7, К-1)

Дизайн-проект интерьера

Стадия	Лист	Листов
РП	13	120

График закупок и работ. Лист 3 из 3

М б/м

Кырлан Александр Сергеевич

01

Архитектурные решения


Кырлан Александр Сергеевич

выпуск 04.11.2026 № 20cec94f32 · стр. 14 из 130

Обмерный план

Существующее положение · размеры в мм · отметки от чистого пола

ПРЕДВАРИТЕЛЬНО · не для производства работ · открыто пунктов: 8 (реестр — л. 6, 7)

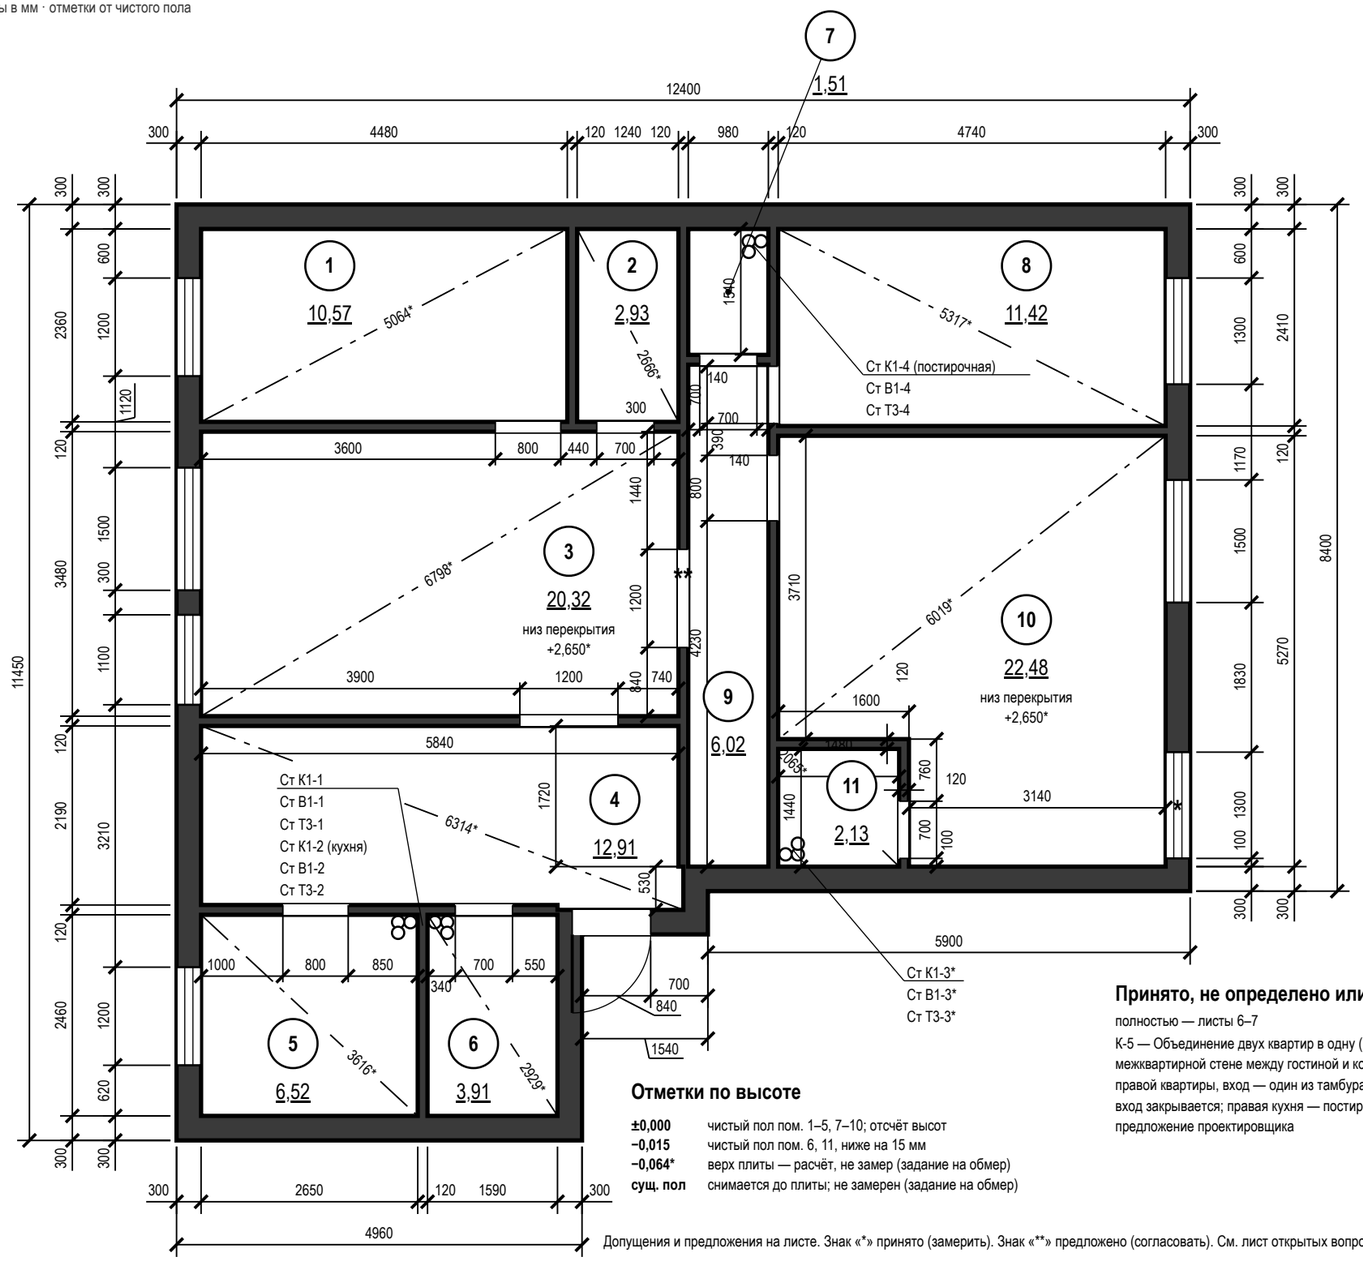

Экспликация помещений

№	Наименование	Площадь, м²
1	Кабинет-библиотека	10,57
2	Кладовая	2,93
3	Гостиная-столовая	20,32
4	Прихожая-холл	12,91
5	Кухня	6,52
6	Ванная	3,91
7	Постирочная	1,51
8	Спальня 2	11,42
9	Коридор	6,02
10	Спальня мастер	22,48
11	Ванная мастер	2,13
	Итого (общая площадь)	**100,72**

Условные обозначения

- существующие стены (сечение)
- окно (рама, остекление)
- проём существующий, без заполнения (откосы)
- стояк: К1 — канализация, В1 — ХВС, Т3 — ГВС
- ** — «**» — предложение проектировщика, заказчиком не утверждено
- диагональ помещения — контроль прямоугольности
- (1) — номер помещения, площадь м²
- * — «*» — принято, не замерено и не подтверждено

Отметки по высоте

±0,000	чистый пол пом. 1–5, 7–10; отсчёт высот
−0,015	чистый пол пом. 6, 11, ниже на 15 мм
−0,064*	верх плиты — расчёт, не замер (задание на обмер)
сущ. пол	снимается до плиты; не замерен (задание на обмер)

Принято, не определено или спорно

полностью — листы 6–7

К-5 — Объединение двух квартир в одну (проём в межквартирной стене между гостиной и коридором правой квартиры, вход — один из тамбура, второй вход закрывается; правая кухня — постирочная) предложение проектировщика

Допущения и предложения на листе. Знак «*» принято (замерить). Знак «**» предложено (согласовать). См. лист открытых вопросов (лист 6).

Примечания

1. Размеры — в мм по чистым поверхностям стен до отделки (по плану заказчика); площади — в м² по тем же размерам. До начала работ выполнить контрольный обмер.
2. Источник плана — допущение, не замер: растровый скан плана заказчика, размеры сняты с размерных цепочек, на объекте не замерены. Реестр: листы 6–7, вопросы К-1, К-6.
3. Знак «*» у проёма — положение не замерено; реестр: листы 6–7, вопрос К-1.
4. Знак «*» у стояка — положение принято, не замерено (Ст К1-3*, Ст В1-3*, Ст Т3-3*); сверить на объекте до разметки. Реестр: листы 6–7, вопрос К-6.
5. За отметку ±0,000 принят чистый пол, не существующий (блок отметок). «Низ перекрытия» у марки помещения — отметка низа перекрытия от ±0,000, как на развёртках и плане потолков (не высота потолка: потолок — по плану потолков); отметка со знаком «*» — принятая, не замер (вопрос К-2).
6. Толщины стен: наружные 300 мм, перегородки 120 мм; отличающиеся толщины и уступы — размерами на плане.
7. Несущие стены не определены: до технического заключения все стены считать несущими; проёмы и штробы в них не выполнять.
8. Дверные проёмы показаны без заполнения (двери — лист 17); высота дверных проёмов 2100 мм, проёмов без двери 2100 мм; низ окон (подоконник) 720, 735, 763, 783, 825 мм от чистого пола, высота окон 1560, 1550, 1552, 1548 мм.
9. Диагонали — контрольные размеры; «*» — расчёт по принятому контуру (К-1), при обмере заменить замеренным; расхождение более 5 мм подписать на плане как перекос.
10. Размеры проверить на месте до начала работ; расхождение контрольных промеров ≤ 2 %.
11. Размеры короче 1 мм на листе цепочкой не показаны (две выносные линии на таком расстоянии сливаются): пом. 9, стена Б — 20 мм от угла до проёма.

1000 мм · печать 1:1

Изм.	Кол.уч	Лист	№ док.	Подп.	Дата
Разраб.		Кырлан А.С.			04.11.26
Пров.					
ГИП					
Н. контр.					
Утв.					

ГД-2026-009-АИ

Квартира 103 м²

Общая площадь 100,72* м² · * размеры со скана, не замерены (реестр — л. 6, 7, К-1)

Дизайн-проект интерьера

Стадия	Лист	Листов
РП	14	120

Обмерный план

М 1:75


Кырлан Александр Сергеевич

выпуск 04.11.2026 № 20cec94f32 · стр. 15 из 130

План демонтажа и монтажа перегородок

Перепланировка не выполняется · существующие стены сохраняются · размеры в мм

ПРЕДВАРИТЕЛЬНО · не для производства работ · открыто пунктов: 8 (реестр — л. 6, 7)

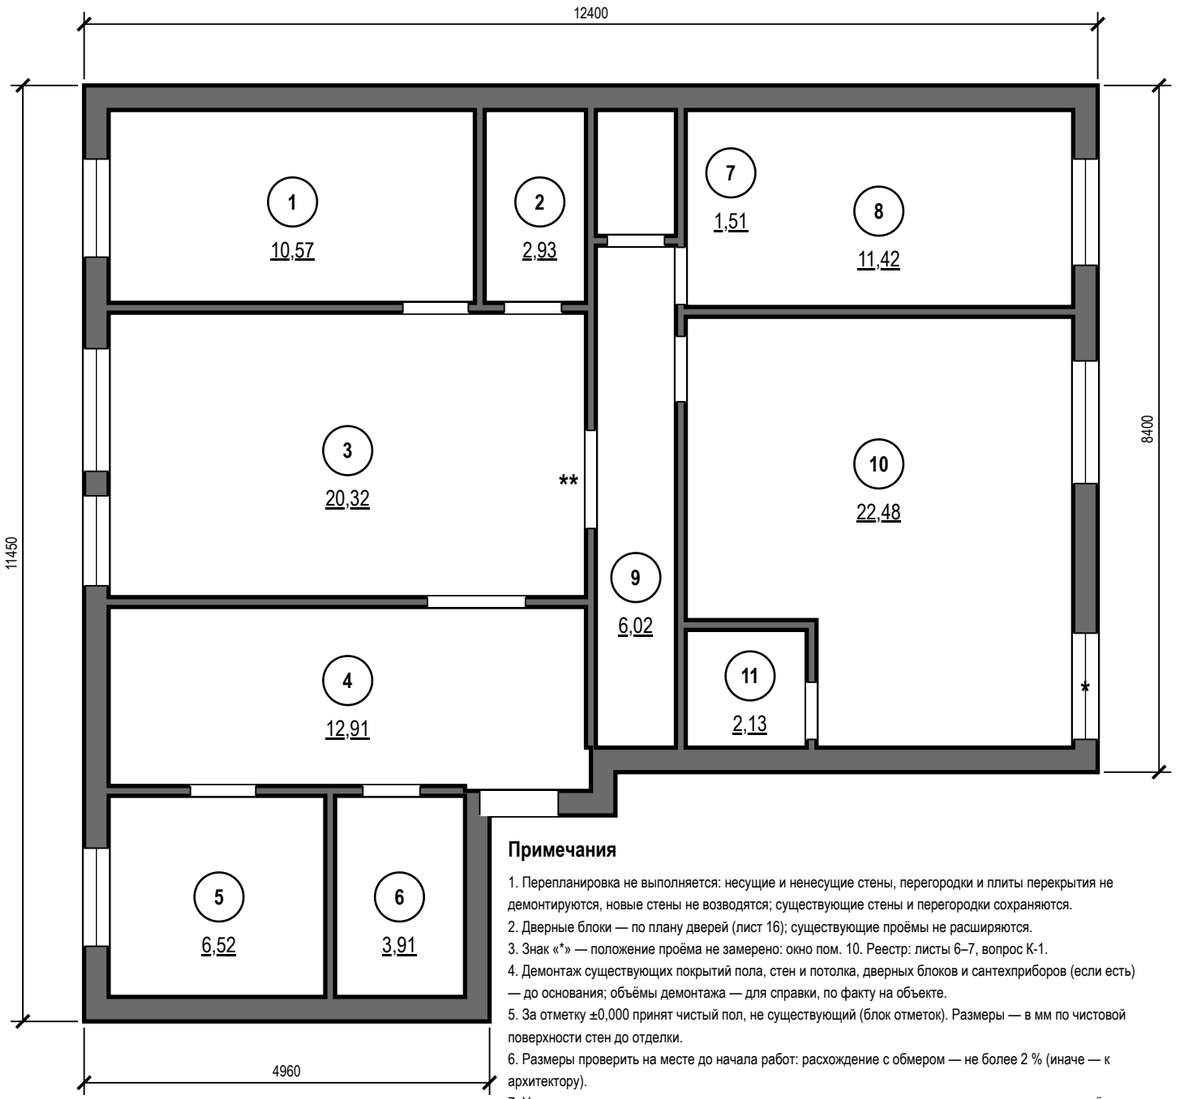

Условные обозначения

- существующие стены — сохраняются;
- несущие не определены — считать несущими
- демонтируемые конструкции — на плане нет
- возводимые перегородки — на плане нет
- проём существующий, без заполнения (откосы)
- (1) номер помещения, площадь м²
- * «*» — принято, не замерено и не подтверждено

Отметки по высоте

±0,000	чистый пол пом. 1–5, 7–10; отсчёт высот	**−0,064***	верх плиты — расчёт, не замер (задание на обмер)
−0,015	чистый пол пом. 6, 11, ниже на 15 мм	**сущ. пол**	снимается до плиты; не замерен (задание на обмер)

Примечания

1. Перепланировка не выполняется: несущие и ненесущие стены, перегородки и плиты перекрытия не демонтируются, новые стены не возводятся; существующие стены и перегородки сохраняются.
2. Дверные блоки — по плану дверей (лист 16); существующие проёмы не расширяются.
3. Знак «*» — положение проёма не замерено: окно пом. 10. Реестр: листы 6–7, вопрос К-1.
4. Демонтаж существующих покрытий пола, стен и потолка, дверных блоков и сантехприборов (если есть) — до основания; объёмы демонтажа — для справки, по факту на объекте.
5. За отметку ±0,000 принят чистый пол, не существующий (блок отметок). Размеры — в мм по чистовой поверхности стен до отделки.
6. Размеры проверить на месте до начала работ: расхождение с обмером — не более 2 % (иначе — к архитектору).
7. Несущие стены не определены: до технического заключения все стены считать несущими — проёмы, ниши и штробы в них не выполнять.

Допущения и предложения на листе

Основа листа: размеры сняты со скана обмерного плана KV design (см): часть подписей не читается, помещения выровнены по читаемым размерам; контрольный обмер не выполнен (К-1); высота потолка 2650 мм принята по отметкам обмера (Н = 2,50…2,66 м, ригель 2,28 м) — уточнить при обмере (К-2); толщины стен 300 / 120 мм приняты, межквартирная стена и колонны — по скану, не замерены (К-1); разрешённая мощность 15 кВт принята по типовым ТУ; при объединении двух квартир — переоформление ТУ (К-4); подрайон климата не задан — принят не северный (жилые от 2,5 м) (К-8).

Знак «*» — принято, не замерено и не подтверждено (замерить на объекте): К-1: окно пом. 10 (стена Б) — Окно 1300 при offset 3500 на стене Б основной части (длина 3830) выходило за стену на 970 мм.

Знак «**» — предложение проектировщика, заказчиком не утверждено (согласовать с заказчиком): К-5: дверь пом. 3 (стена Б) — проём в межквартирной стене — объединение квартир, предложение до техзаключения.

См. лист открытых вопросов (лист 6, записи К-1, К-2, К-4, К-5, К-8).

1000 мм · печать 1:1

Изм.	Кол.уч	Лист	№ док.	Подп.	Дата
Разраб.		Кырлан А.С.			04.11.26
Пров.					
ГИП					
Н. контр.					
Утв.					

ГД-2026-009-АИ

Квартира 103 м²

Общая площадь 100,72* м² · * размеры со скана, не замерены (реестр — л. 6, 7, К-1)

Дизайн-проект интерьера

Стадия	Лист	Листов
РП	15	120


План демонтажа и монтажа перегородок

М 1:75

Кырлан Александр Сергеевич

План дверей

Проёмы, марки заполнения, привязки · размеры в мм

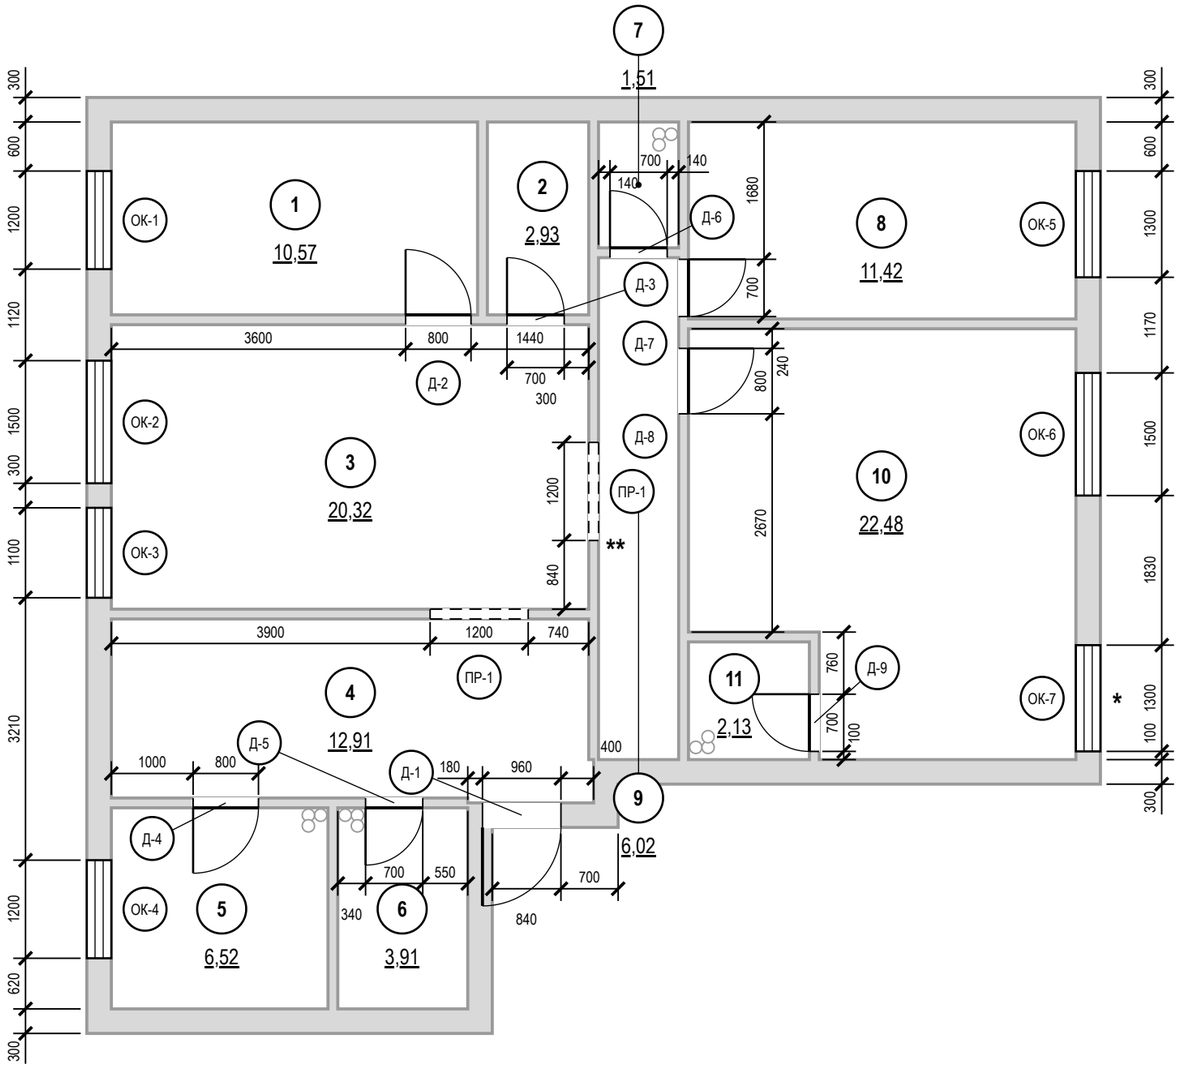

Условные обозначения

- стены (подложка обмера)
- дверь распашная, дуга открывания
- дверь скрытого монтажа
- дверь входная (полотно толще)
- портал (штрих — перемычка)
- оконный блок
- Д — марка типа (Д-N, ПР-N, ОК-N)
- 1 — номер помещения, площадь м²
- * — «*» — принято, не замерено и не подтверждено
- ** — «**» — предложение проектировщика, заказчиком не утверждено

Примечания

1. Размеры проёмов и привязки — в миллиметрах от чистых граней стен до отделки; привязка — от угла того помещения, со стороны которого стоит размер. Размер проёма — ширина × высота от чистого пола 0,000. Размеры на плане — проёмов, не полотен: полотно — в ведомости, коробка — по системе. Откос от угла помещения до проёма с коробкой — не менее 50 мм.
2. Марки в кружках — типы заполнения проёмов (ГОСТ 21.501-2018, п. 5.3.2); одна марка — один типоразмер; количество сверено с планом.
3. Д-2…Д-9 — существующие проёмы, до техзаключения не расширять.
4. Д-1: дуга наружу — по плану заказчика, не проверено; блок оставить или заменить — не решено.
5. Размеры проёмов и привязки сняты со скана плана заказчика и на объекте не замерены (обмерный план — лист 14).
6. Знак «*» у проёма — допущение: положение проёма не замерено (окно пом. 10, стена Б); размер напечатан как принятый; в ведомости — знак «*» в графе «Прим.». Реестр: листы 6–7, вопрос К-1.
7. Экспликация помещений — лист 14; в марках помещений — номер и площадь, м².
8. Ведомость заполнения проёмов, открывание полотен, заказ и порядок монтажа блоков — лист 17.
9. Привязка проёма к углу помещения меньше 1 мм на листе, размер на плане не показан: Д-7 — 30 мм.

Допущения и предложения на листе

Основа листа: размеры сняты со скана обмерного плана KV design (см): часть подписей не читается, помещения выровнены по читаемым размерам; контрольный обмер не выполнен (К-1); высота потолка 2650 мм принята по отметкам обмера (Н = 2,50…2,66 м, ригель 2,28 м) — уточнить при обмере (К-2); толщины стен 300 / 120 мм приняты, межквартирная стена и колонны — по скану, не замерены (К-1); разрешённая мощность 15 кВт принята по типовым ТУ; при объединении двух квартир — переоформление ТУ (К-4); подрайон климата не задан — принят не северный (жилые от 2,5 м) (К-8).

Знак «*» — принято, не замерено и не подтверждено (замерить на объекте): К-1: окно пом. 10 (стена Б) — Окно 1300 при offset 3500 на стене Б основной части (длина 3830) выходило за стену на 970 мм; К-6: Ст К1-3, Ст В1-3, Ст Т3-3 — положение снято со скана обмера, отдельно не замерялось; ось внутри габарита поддона См1 — обмер угла по К-6.

Знак «**» — предложение проектировщика, заказчиком не утверждено (согласовать с заказчиком): К-5: дверь пом. 3 (стена Б) — проём в межквартирной стене — объединение квартир, предложение до техзаключения.

Изменения по листу без подписи: ИЗ-1.

См. лист открытых вопросов (лист 6, записи ИЗ-1, К-1, К-2, К-4–К-6, К-8).

1000 мм · печать 1:1

Изм.	Кол.уч	Лист	№ док.	Подп.	Дата
Разраб.		Кырлан А.С.			04.11.26
Пров.					
ГИП					
Н. контр.					
Утв.					

ГД-2026-009-АИ

Квартира 103 м²

Общая площадь 100,72* м² · * размеры со скана, не замерены (реестр — л. 6, 7, К-1)

Дизайн-проект интерьера

Стадия	Лист	Листов
РП	16	120

План дверей

М 1:75

Кырлан Александр Сергеевич


Ведомость заполнения проёмов

Проёмы, полотна, отделка, фурнитура · размеры в мм

Ведомость заполнения проёмов

Марка	Наименование, обозначение	Проём ш×в, мм	Полотно (расч.)	Кол.	Откр.	Отделка полотна	Фурнитура	Прим.
Д-1	Блок дверной входной, ГОСТ 31173-2016	960×2100	блок задать	1	Л	в комплекте блока	в комплекте блока (замки, глазок)	наружу
Д-2	Дверь скрытого монтажа, UNION FILO-60 Piatto	800×2100	700×2000	1	П	окраска No. 291 с двух сторон	скрытые петли 3D, магнитный замок	
Д-3	Дверь скрытого монтажа, UNION FILO-60 Piatto	700×2100	600×2000	1	П	S 0502-Y — пом. 2, No. 291 — пом. 3	скрытые петли 3D, магнитный замок	
Д-4	Дверь скрытого монтажа, UNION FILO-60 Piatto	800×2100	700×2000	1	Л	окраска No. 291 с двух сторон	скрытые петли 3D, магнитный замок	
Д-5	Дверь скрытого монтажа, UNION FILO-60 Piatto	700×2100	600×2000	1	Л	в тон облицовки — пом. 6, No. 291 — пом. 4	скрытые петли 3D, магнитный замок, фиксатор WC	порог 15
Д-6	Дверь скрытого монтажа, UNION FILO-60 Piatto	700×2100	600×2000	1	П	S 0502-Y — пом. 7, No. 291 — пом. 9	скрытые петли 3D, магнитный замок	
Д-7	Дверь скрытого монтажа, UNION FILO-60 Piatto	700×2100	600×2000	1	П	окраска No. 291 с двух сторон	скрытые петли 3D, магнитный замок	
Д-8	Дверь скрытого монтажа, UNION FILO-60 Piatto	800×2100	700×2000	1	П	окраска No. 291 с двух сторон	скрытые петли 3D, магнитный замок	
Д-9	Дверь скрытого монтажа, UNION FILO-60 Piatto	700×2100	600×2000	1	Л	в тон облицовки — пом. 11, No. 291 — пом. 10	скрытые петли 3D, магнитный замок, фиксатор WC	порог 15
ПР-1	Портал без заполнения	1200×2100		2				** пом. 3; б/п
ОК-1	Блок оконный, ГОСТ 23166-2021; стекло — триплекс	1200×1560		1				низ 720
ОК-2	Блок оконный, ГОСТ 23166-2021; стекло — триплекс	1500×1550		1				низ 735
ОК-3	Блок оконный, ГОСТ 23166-2021; стекло — триплекс	1100×1550		1				низ 735
ОК-4	Блок оконный, ГОСТ 23166-2021; стекло — триплекс	1200×1550		1				низ 763
ОК-5	Блок оконный, ГОСТ 23166-2021; стекло — триплекс	1300×1552		1				низ 783
ОК-6	Блок оконный, ГОСТ 23166-2021; стекло — триплекс	1500×1548		1				низ 825
ОК-7	Блок оконный, ГОСТ 23166-2021; стекло — триплекс	1300×1548		1				* пом. 10; низ 825

Схемы дверных блоков (1:75) — вид со стороны открывания; вершина треугольника — сторона петель

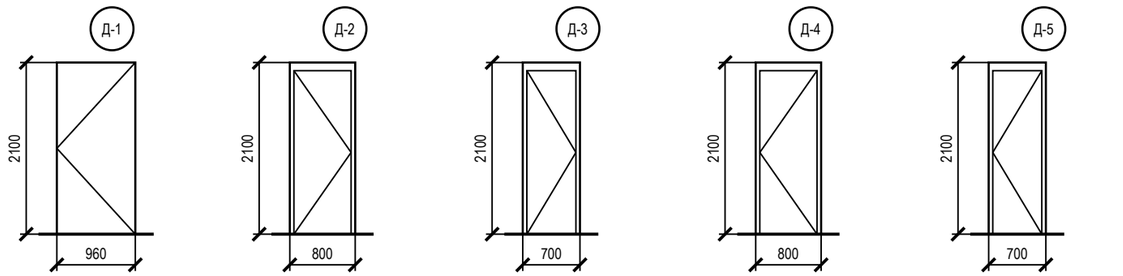

Допущения и предложения на листе

Основа листа: размеры сняты со скана обмерного плана KV design (см): часть подписей не читается, помещения выровнены по читаемым размерам; контрольный обмер не выполнен (К-1); высота потолка 2650 мм принята по отметкам обмера (Н = 2,50…2,66 м, ригель 2,28 м) — уточнить при обмере (К-2); толщины стен 300 / 120 мм приняты, межквартирная стена и колонны — по скану, не замерены (К-1); разрешённая мощность 15 кВт принята по типовым ТУ; при объединении двух квартир — переоформление ТУ (К-4); подрайон климата не задан — принят не северный (жилые от 2,5 м) (К-8).

См. лист открытых вопросов (лист 6, записи К-1, К-2, К-4, К-8).

Примечания

1. Марки проёмов — те же, что на плане размещения дверей (лист 16); привязки проёмов — там же.
2. Открывание: Л — петли слева, П — справа, если смотреть со стороны, куда открывается полотно (на себя).
3. Остекление окон: ОК-1 (пом. 1) — триплекс; ОК-2 (пом. 3) — триплекс; ОК-3 (пом. 3) — триплекс; ОК-4 (пом. 5) — триплекс; ОК-5 (пом. 8) — триплекс; ОК-6 (пом. 10) — триплекс; ОК-7 (пом. 10) — триплекс. Тип стекла указать при заказе оконных блоков; замена на другое стекло — только по согласованию с автором проекта.
4. ОК-1, ОК-2, ОК-3, ОК-4, ОК-5, ОК-6, ОК-7: низ остекления 720 и 735 и 763 и 783 и 825 мм — ниже 900 мм от чистого пола, поэтому окно заказывать с безопасным стеклом (триплекс); ограждение проёма в проекте не задано (СП 54.13330.2022, п. 6.4.9; ГОСТ Р 56926).
5. Скрытые двери (Д-2…Д-9): проём замерить в чистоте; блок заказать до штукатурки (≈ 30 дн.), короб ставить до штукатурки; полотно навесить после чистовой отделки, красить в цвет стен. Порядок — практика монтажа, изготовитель подтверждает.
6. Полотно «расч.» — по проёму и ряду изделия с запасом по каталогам, заказ — по таблице проёмов модели; Д-2…Д-9: проём 2100, а под полотно 2000 по каталогам нужен 2050–2080, под 2100 — 2150–2180: высоту проёма — по модели; Д-1: входной блок по ГОСТ 31173-2016 — задать при выборе блока.

Изм.	Кол.уч	Лист	№ док.	Подп.	Дата			
Разраб.		Кырлан А.С.			04.11.26	ГД-2026-009-АИ		
Пров.						Квартира 103 м²		
ГИП						Общая площадь 100,72* м² · * размеры со скана, не замерены (реестр — л. 6, 7, К-1)		
						Дизайн-проект интерьера	Стадия: РП; Лист: 17; Листов: 120	
Н. контр.						Ведомость заполнения проёмов	Кырлан Александр Сергеевич	
Утв.						М б/м		

выпуск 04.11.2026 № 20cec94f32 · стр. 18 из 130

02

Планировочное решение

Кырлан Александр Сергеевич

выпуск 04.11.2026 № 20cec94f32 · стр. 19 из 130

Концепция интерьера


Мид-сенчури · схема комплементарная · 60/30/10 · материалы, образы и зонирование

ПРЕДВАРИТЕЛЬНО · не для производства работ · открыто пунктов: 8 (реестр — л. 6, 7)

Идея

Стиль — мид-сенчури: оптимизм, функциональность, тёплое дерево, лёгкость, ретро без китча, связь с улицей, графичные акценты. Модернизм середины века 65 % + ар-деко 35 %. Стены — School House White No. 291, потолки белый S 0502-Y; второй план — орех и тик, оливковый Bancha No. 298, сине-серый Inchyra Blue No. 289; акценты горчица S 2050-Y20R, терракота S 3050-Y70R, тил S 5030-B10G, изумрудный бархат S 5040-B90G; металл — латунь. Мебель — авторские модели середины века (как предложение, модели уточняются с заказчиком). Цветовая схема комплементарная, пропорция 60/30/10: база на стенах и потолках, вторичный цвет — в текстиле и мягкой мебели, акцент — точечно.

Мудборд: материалы и фактуры

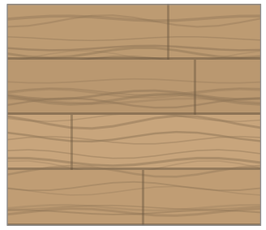

1167-4250
пол



A8UZ
пол, стены



Белый с лёгкой желтизной · NCS S 0502-Y
потолок, стены, плинтус




School House White — тёплый меловой белый · Farrow & Ball No. 291
стены, плинтус, потолок




Inchyra Blue — тёмный сине-серый · Farrow & Ball No. 289
акцент (стена А)



Tanner's Brown — тёмный шоколад · Farrow & Ball No. 255
акцент (стена А)

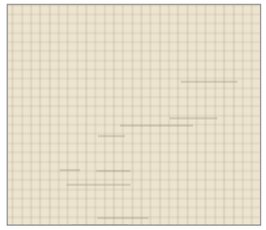

Лён, NCS S 1005-Y20R
портьеры-волна, Портьеры-волна

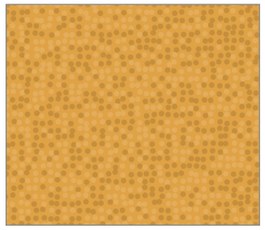

Шерсть, NCS S 2050-Y20R
ковёр под рабочей зоной, ковёр под кроватью



Бархат, Farrow & Ball No. 255
Подушки декоративные на диван

Палитра 60/30/10



60 % база — Farrow & Ball No. 291 School House White — тёплый меловой белый, LRV 73; NCS S 0502-Y Белый с лёгкой желтизной, LRV 95

30 % вторичный — Farrow & Ball No. 298 Bancha — оливковый середины века, LRV 14; Farrow & Ball No. 289 Inchyra Blue — тёмный сине-серый, LRV 13; Farrow & Ball No. 255 Tanner's Brown — тёмный шоколад, LRV 7

10 % акцент — NCS S 2050-Y20R Горчичный, LRV 42; NCS S 3050-Y70R Терракотовый / жжёный оранжевый, LRV 18; NCS S 5030-B10G Тил, LRV 12; NCS S 5040-B90G Изумрудный, LRV 8

Функциональное зонирование (М 1:200)



- дневная зона: гостиная, кухня, столовая
- ночная зона: спальни
- мокрая зона: санузлы
- хранение: гардеробная, кладовая
- вход и коммуникации
- функциональная зона в помещении
- (1) номер помещения (лист 19)

Образы помещений

3. Гостиная-столовая — 20,32 м²
стены Farrow & Ball No. 291; акцент No. 255 на стене А

5. Кухня — 6,52 м²
стены Farrow & Ball No. 291
пол — 1167-4250

8. Спальня 2 — 11,42 м²
стены Farrow & Ball No. 291; акцент No. 289 на стене А

10. Спальня мастер — 22,48 м²
стены Farrow & Ball No. 291; акцент No. 289 на стене А

1. Кабинет-библиотека — 10,57 м²
стены Farrow & Ball No. 291; акцент No. 289 на стене А

4. Прихожая-холл — 12,91 м²
стены Farrow & Ball No. 291
пол — A8UZ

9. Коридор — 6,02 м²
стены Farrow & Ball No. 291
пол — 1167-4250

7. Постирочная — 1,51 м²
стены NCS S 0502-Y
пол — 1167-4250

6. Ванная — 3,91 м²
стены Atlas Concorde A8UZ
пол — Atlas Concorde Marvel Travertine Sand

11. Ванная мастер — 2,13 м²
стены Atlas Concorde A8UZ
пол — Atlas Concorde Marvel Travertine Sand

2. Кладовая — 2,93 м²
стены NCS S 0502-Y
пол — 1167-4250

Материалы и отделка

1167-4250
пол — пом. 1, 2, 3, 5, 7, 8, 9, 10

A8UZ
пол, стены — пом. 4, 6, 11

Керамогранит матовый
тон F497; 600×600
фартук — пом. 5

Atlas Concorde Marvel Travertine Sand Cross 60×60 Matte Sensitech
арт. AFUL (той же коллекции, что стены A8UZ; тон сверить по образцу); Atlas Concorde Marvel Travertine Sand Cross 60×60 Matte Sensitech
пол — пом. 6, 11

Farrow & Ball No. 291 School House White — тёплый меловой белый, LRV 73
Farrow & Ball Modern Emulsion, матовая
стены, плинтус, потолок — пом. 1, 3, 4, 5, 8, 9, 10

NCS S 0502-Y Белый с лёгкой желтизной, LRV 95
Tikkurila Anti-Reflex 2, глубокоматовая
потолок, стены, плинтус — пом. 1, 2, 4, 6, 7, 8, 9, 10, 11

Farrow & Ball No. 289 Inchyra Blue — тёмный сине-серый, LRV 13
акцентная стена
акцент (стена А) — пом. 1, 8, 10

Farrow & Ball No. 255 Tanner's Brown — тёмный шоколад, LRV 7
акцентная стена
акцент (стена А) — пом. 3

Текстиль и металл

Лён, NCS S 1005-Y20R
портьеры-волна, Портьеры-волна

Шерсть, NCS S 2050-Y20R
ковёр под рабочей зоной, ковёр под кроватью

Шерсть, Farrow & Ball No. 289
плед на кровать

Шерсть, Farrow & Ball No. 298
ковёр мягкой группы, ковёр под кроватью

Шерсть, Farrow & Ball No. 255
Плед на диван

Вуаль, NCS S 0502-Y
тюль

Букле, NCS S 3050-Y70R
подушки декоративные на кровать

Вуаль, Farrow & Ball No. 291
Тюль-вуаль

Бархат, Farrow & Ball No. 255
Подушки декоративные на диван

Чёрный матовый металл
зеркало, зеркало в рост

Чего избегаем

1) Ретро-парк: все акценты сразу (оранжевый + бирюза + горчица + атомные обои) — это тематический кафе-интерьер
2) Дешёвые реплики с неправильными пропорциями (толстые прямые ножки, утяжелённые спинки)
3) Холодный серо-белый сканди с ламинатом под беленый дуб — у мид-сенчури тёплое тёмное дерево
4) Лепнина, многоуровневые потолки, глянец и тяжёлые шторы с ламбрекенами
5) Сплошной тик: дерево на полу, стенах, мебели и потолке одного тона — нужен контраст светлых стен
6) Только винтаж без современной эргономики (кухни, хранение) — стиль ценил функциональность

Допущения и предложения на листе. Основа листа: размеры сняты со скана обмерного плана KV design (см): часть подписей не читается, помещения выровнены по читаемым размерам; контрольный обмер не выполнен (К-1); высота потолка 2650 мм принята по отметкам обмера (Н = 2,50…2,66 м, ригель 2,28 м) — уточнить при обмере (К-2); толщины стен 300 / 120 мм приняты, межквартирная стена и колонны — по скану, не замерены (К-1); разрешённая мощность 15 кВт принята по типовым ТУ; при объединении двух квартир — переоформление ТУ (К-4); подрайон климата не задан — принят не северный (жилые от 2,5 м) (К-8). См. лист открытых вопросов (лист 6, записи К-1, К-2, К-4, К-8).

Примечания

1. Коды цвета — по веерам производителей (колерная карта, лист 57); перед закупкой краски — выкрас на стене объекта под дневным светом и лампами проекта.
2. Материалы — по ведомости отделки (лист 54); мебель, текстиль и декор — по спецификации (лист 20). Образцы доски, керамогранита и тканей утвердить до заказа.
3. Фактуры на листе условные, цвет передан по HEX-значениям производителей: при печати возможны отклонения, решение — только по физическому образцу.

Изм.	Кол.уч	Лист	№ док.	Подп.	Дата
Разраб.		Кырлан А.С.			04.11.26
Пров.					
ГИП					
Н. контр.					
Утв.					

ГД-2026-009-АИ

Квартира 103 м²

Общая площадь 100,72* м² · * размеры со скана, не замерены (реестр — л. 6, 7, К-1)

Дизайн-проект интерьера

Стадия	Лист	Листов
РП	18	120


Концепция интерьера
М б/м

Кырлан Александр Сергеевич

выпуск 04.11.2026 № 20cec94f32 · стр. 20 из 130

План расстановки мебели

Мебель и оборудование · размеры в мм от чистовых стен · марки — по ведомости

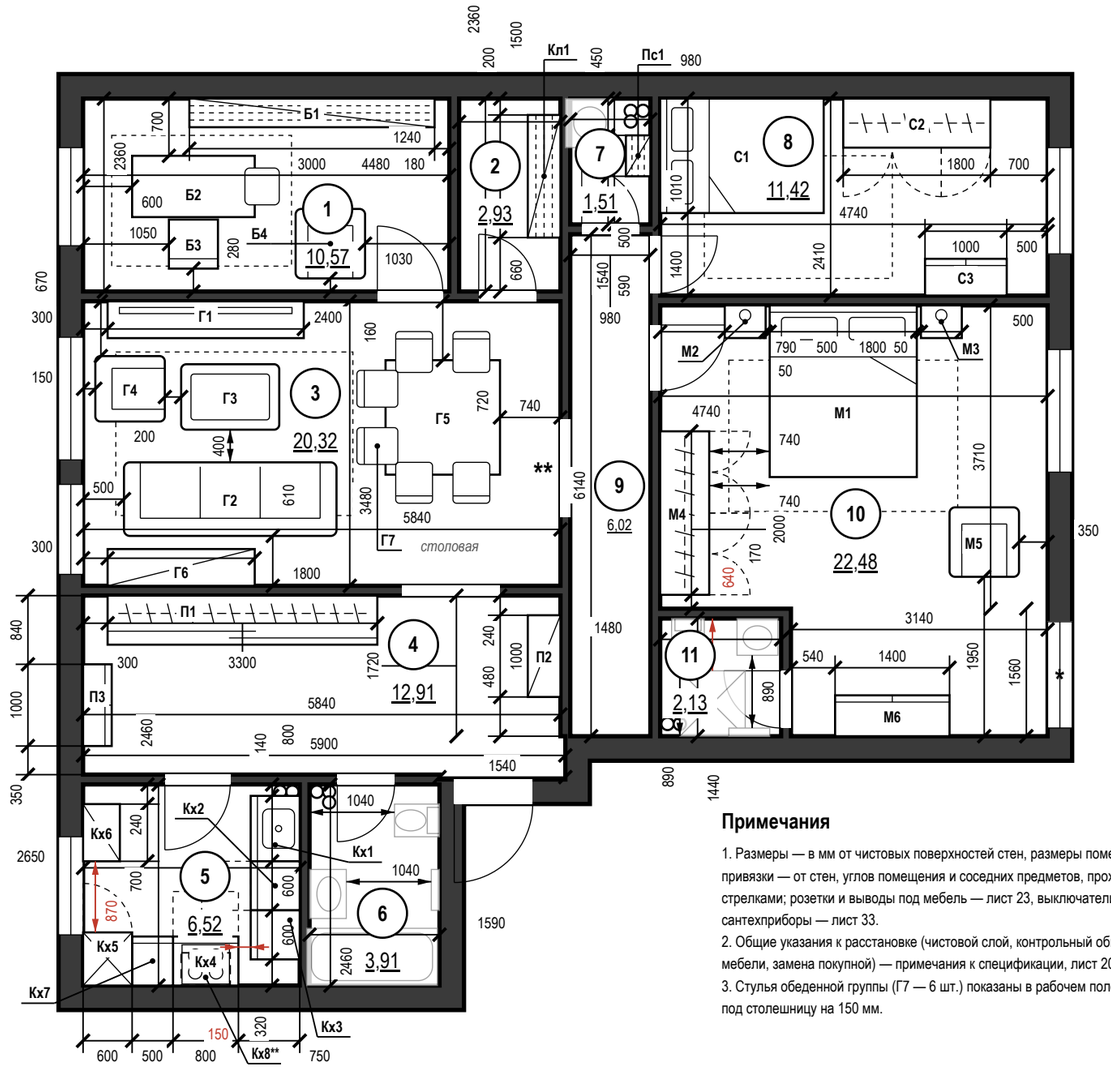

Примечания

1. Размеры — в мм от чистовых поверхностей стен, размеры помещений — в свету, привязки — от стен, углов помещения и соседних предметов, проходы и зазоры стрелками; розетки и выводы под мебель — лист 23, выключатели — лист 25, сантехприборы — лист 33.
2. Общие указания к расстановке (чистовой слой, контрольный обмер, зазоры встроенной мебели, замена покупной) — примечания к спецификации, лист 20.
3. Стулья обеденной группы (Г7 — 6 шт.) показаны в рабочем положении, задвинутыми под столешницу на 150 мм.

Условные обозначения

- мебель и оборудование — габарит в масштабе
- навесные шкафы (низ выше 0,9 м) — невидимый контур
- ковёр
- зона открывания дверец шкафов и техники
- К1 — марка предмета по ведомости мебели
- привязка от чистовой стены, мм
- ширина прохода, зазор, мм
- проход меньше нормы — расстановку изменить
- сантехприборы — подложка (лист ВК)
- существующие стены (сечение)
- * — «*» — принято, не замерено и не подтверждено
- ** — «**» — предложение проектировщика, заказчиком не утверждено
- стояк: К1 — канализация, В1 — ХВС, Т3 — ГВС
- 1 — номер помещения, площадь м²
- *зона* — функциональная зона помещения

Допущения и предложения на листе

Основа листа: размеры сняты со скана обмерного плана KV design (см): часть подписей не читается, помещения выровнены по читаемым размерам; контрольный обмер не выполнен (К-1); высота потолка 2650 мм принята по отметкам обмера (Н = 2,50…2,66 м, ригель 2,28 м) — уточнить при обмере (К-2); толщины стен 300 / 120 мм приняты, межквартирная стена и колонны — по скану, не замерены (К-1); разрешённая мощность 15 кВт принята по типовым ТУ; при объединении двух квартир — переоформление ТУ (К-4); подрайон климата не задан — принят не северный (жилые от 2,5 м) (К-8).
Знак «*» — принято, не замерено и не подтверждено (замерить на объекте): К-1: окно пом. 10 (стена Б) — Окно 1300 при offset 3500 на стене Б основной части (длина 3830) выходило за стену на 970 мм; К-6: Ст К1-3, Ст В1-3, Ст Т3-3 — положение снято со скана обмера, отдельно не замерялось; ось внутри габарита поддона См1 — обмер угла по К-6.
Знак «**» — предложение проектировщика, заказчиком не утверждено (согласовать с заказчиком): Кх8 — над индукционной панелью Кх4 нужна вытяжка: в составе кухни её не было, розетка вытяжки образца висела без потребителя; К-5: дверь пом. 3 (стена Б) — проём в межквартирной стене — объединение квартир, предложение до техзаключения.
Открытые вопросы и конфликты по листу: К-1.
См. лист открытых вопросов (лист 6, записи К-1, К-2, К-4–К-6, К-8).

1000 мм · печать 1:1

ПРЕДВАРИТЕЛЬНО · не для производства работ · открыто пунктов: 8 (реестр — л. 6, 7)

Экспликация помещений

лист 14 · на плане — номера в марках

Ведомость мебели и оборудования

Марка	Наименование	Ш×Г×В, мм	Пом.	Кол.
Б1	Стеллаж-библиотека из ореха	3000×350×2400	1	1
Б2	Письменный стол-бюро середины века	750×1500×750	1	1
Б3	Стул рабочий с подлокотниками	600×600×800	1	1
Б4	Кресло-лаунж с оттоманкой	850×850×850	1	1
Кл1	Стеллаж для хранения	1500×400×2400	2	1
Г1	ТВ-консоль из ореха	2400×450×550	3	1
Г2	Диван середины века	2600×900×780	3	1
Г3	Стол журнальный	1200×800×400	3	1
Г4	Кресло	800×850×1070	3	1
Г5	Стол обеденный на одной ножке	1400×1400×730	3	1
Г6	Буфет-сервант из ореха	1800×450×750	3	1
П1	Шкаф-купе	3300×600×2450	4	1
П2	Банкетка	1000×400×450	4	1
П3	Консоль ар-деко	1000×350×800	4	1
Кх1	Модуль под мойку	800×600×900	5	1
Кх2	Посудомоечная машина встроенная	600×600×900	5	1
Кх3	Модуль с ящиками	600×600×900	5	1
Кх4	Модуль с варочной панелью	800×600×900	5	1
Кх7	Модуль с ящиками между	500×600×900	5	1
Кх5	Колонна с холодильником	600×650×2100	5	1
Кх6	Стол барный у окна	700×450×900	5	1
Кх8**	Вытяжка над варочной панелью	600×400×600	5	1
Пс1	Полки для хранения	500×300×2000	7	1
С1	Кровать 1400×2000	1400×2000×450	8	1
С2	Шкаф распашной	1800×600×2400	8	1
С3	Туалетный столик середины века	1000×450×750	8	1
М1	Кровать 1800×2100	1800×2100×450	10	1
М2	Тумба прикроватная	500×400×550	10	1
М3	Тумба прикроватная	500×400×550	10	1
М4	Шкаф распашной	2000×600×2400	10	1
М5	Кресло-лаунж с оттоманкой	850×850×850	10	1
М6	Комод ар-деко	1400×500×800	10	1
Г7	Стул обеденный к столу Г5	450×500×820	3	6

Ш — вдоль стены (изголовья), Г — от стены (длина кровати)
Материалы, модели, допуск замены — лист 20

Изм.	Кол.уч	Лист	№ док.	Подп.	Дата
Разраб.		Кырлан А.С.			04.11.26
Пров.					
ГИП					
Н. контр.					
Утв.					

ГД-2026-009-АИ

Квартира 103 м²

Общая площадь 100,72* м² · * размеры со скана, не замерены (реестр — л. 6, 7, К-1)

Дизайн-проект интерьера

Стадия	Лист	Листов
РП	19	120

План расстановки мебели

М 1:75

Кырлан Александр Сергеевич

выпуск 04.11.2026 · № 20cec94f32 · стр. 21 из 130

Спецификация мебели и оборудования

ПРЕДВАРИТЕЛЬНО · не для производства работ · открыто пунктов: 8 (реестр — л. 6, 7)

Форма 1 ГОСТ 21.110-2013 · позиции мебели — по плану расстановки

Поз.	Наименование и техническая характеристика	Тип, марка, обозначение документа, опросного листа	Код продукции	Поставщик	Ед. измерения	Кол.	Масса 1 ед., кг	Примечание
	Мебель встроенная и корпусная (изготовление по чертежам мебельщика)							
Кл1	Стеллаж для хранения; каркас и полки — ЛДСП декор «орех» 16 мм; без фасадов; Ш×Г×В 1500×400×2400 мм			изготовление на заказ	шт.	1		пом. 2
П1	Шкаф-купе; корпус ЛДСП 16 мм; фасады — МДФ, шпон ореха 10 мм, масло матовое в профиле: латунь; Ш×Г×В 3300×600×2450 мм			изготовление на заказ	шт.	1		пом. 4
Кх1	Модуль под мойку; корпус ЛДСП 16 мм; фасады — МДФ, шпон ореха 18 мм, масло матовое; Ш×Г×В 800×600×900 мм			изготовление на заказ	шт.	1		пом. 5
Кх2	Модуль под встраиваемую ПММ 60; без корпуса (ниша между соседними модулями); фасад на дверь машины — МДФ 18 мм, эмаль матовая; цоколь; цвет фасадов — в цвет стен (Farrow & Ball No. 291); Ш×Г×В 600×600×900 мм			изготовление на заказ	шт.	1		пом. 5
Кх3	Модуль с ящиками; корпус ЛДСП 16 мм; фасады — МДФ 18 мм, эмаль матовая; цвет фасадов — в цвет стен (Farrow & Ball No. 291); Ш×Г×В 600×600×900 мм			изготовление на заказ	шт.	1		пом. 5
Кх4	Модуль с варочной панелью (индукция) и духовым шкафом; корпус ЛДСП 16 мм; фасады — МДФ 18 мм, эмаль матовая; цвет фасадов — в цвет стен (Farrow & Ball No. 291); Ш×Г×В 800×600×900 мм			изготовление на заказ	шт.	1		пом. 5
Кх5	Колонна с холодильником, ретро-фасад; корпус ЛДСП 16 мм; фасады — МДФ эмаль 18 мм, матовая; цвет — тил; Ш×Г×В 600×650×2100 мм			изготовление на заказ	шт.	1		пом. 5
Кх7	Модуль с ящиками между колонной и плитой; корпус ЛДСП 16 мм; фасады — МДФ 18 мм, эмаль матовая; цвет фасадов — в цвет стен (Farrow & Ball No. 291); Ш×Г×В 500×600×900 мм			изготовление на заказ	шт.	1		пом. 5
Кх8**	Вытяжка над варочной панелью; корпус ЛДСП 16 мм; фасады — МДФ 18 мм, эмаль матовая; цвет фасадов — в цвет стен (Farrow & Ball No. 291); Ш×Г×В 600×400×600 мм			изготовление на заказ	шт.	1		пом. 5
Пс1	Полки для хранения (стена Б, в стороне от короба стояков); каркас и полки — ЛДСП 16 мм, декор «дуб натуральный»; без фасадов; Ш×Г×В 500×300×2000 мм			изготовление на заказ	шт.	1		пом. 7
С2	Шкаф распашной, латунные ручки; корпус ЛДСП 16 мм; фасады — МДФ, шпон ореха 18 мм, масло матовое; Ш×Г×В 1800×600×2400 мм			изготовление на заказ	шт.	1		пом. 8
М4	Шкаф распашной; корпус ЛДСП 16 мм; фасады — МДФ, шпон ореха 18 мм, масло матовое; вставка — латунь; Ш×Г×В 2000×600×2400 мм			изготовление на заказ	шт.	1		пом. 10
	Мебель покупная							
Б1	Стеллаж-библиотека из ореха на всю стену, латунные полкодержатели; шпон, дуб натуральный, матовое масло; Ш×Г×В 3000×350×2400 мм			аналог по характеристикам	шт.	1		пом. 1; замена ≤ габарита
Б2	Письменный стол-бюро середины века, орех, конические ножки; шпон, дуб натуральный, матовое масло; Ш×Г×В 750×1500×750 мм			аналог по характеристикам	шт.	1		пом. 1; замена ≤ габарита
Б3	Стул рабочий с подлокотниками, гнутая фанера и кожа; обивка — ткань, цвет Farrow & Ball No. 298; каркас — дуб натуральный; Ш×Г×В 600×600×800 мм			аналог по характеристикам	шт.	1		пом. 1; замена ≤ габарита
Б4	Кресло-лаунж с оттоманкой (в духе Eames Lounge Chair), палисандровый шпон, чёрная кожа; обивка — ткань, цвет Farrow & Ball No. 298; Ш×Г×В 850×850×850 мм			аналог по характеристикам	шт.	1		пом. 1; замена ≤ габарита
Г1	ТВ-консоль из ореха на конических ножках, ТВ на стене; шпон, дуб натуральный, матовое масло; Ш×Г×В 2400×450×550 мм			аналог по характеристикам	шт.	1		пом. 3; замена ≤ габарита
Г2	Диван середины века (в духе Florence Knoll), букле горчичного цвета, латунные опоры; обивка — ткань, цвет Farrow & Ball No. 298; Ш×Г×В 2600×900×780 мм			аналог по характеристикам	шт.	1		пом. 3; замена ≤ габарита
Г3	Стол журнальный (в духе Noguchi Coffee Table), орех и стекло; шпон, дуб натуральный, матовое масло; Ш×Г×В 1200×800×400 мм			аналог по характеристикам	шт.	1		пом. 3; замена ≤ габарита
Г4	Кресло (в духе Egg Chair), изумрудный бархат; обивка — ткань, цвет Farrow & Ball No. 298; Ш×Г×В 800×850×1070 мм			аналог по характеристикам	шт.	1		пом. 3; замена ≤ габарита
Г5	Стол обеденный на одной ножке (в духе Tulip Table), мрамор Calacatta, d 1400; шпон, дуб натуральный, матовое масло; Ш×Г×В 1400×1400×730 мм			аналог по характеристикам	шт.	1		пом. 3; замена ≤ габарита
Г6	Буфет-сервант из ореха на конических ножках, раздвижные двери; шпон, дуб натуральный, матовое масло; Ш×Г×В 1800×450×750 мм			аналог по характеристикам	шт.	1		пом. 3; замена ≤ габарита
Г7	Стул обеденный к столу Г5; обивка — ткань, цвет Farrow & Ball No. 298; каркас — дуб натуральный; Ш×Г×В 450×500×820 мм			аналог по характеристикам	шт.	6		пом. 3; замена ≤ габарита
П2	Банкетка, изумрудный бархат, латунные ножки; Ш×Г×В 1000×400×450 мм			аналог по характеристикам	шт.	1		пом. 4; замена ≤ габарита
П3	Консоль ар-деко, чёрный лак и латунь; шпон, дуб натуральный, матовое масло; Ш×Г×В 1000×350×800 мм			аналог по характеристикам	шт.	1		пом. 4; замена ≤ габарита

Примечания

1. Позиции мебели совпадают с марками на плане расстановки (лист 19); размеры Ш×Г×В — Ш вдоль стены, Г от стены.
2. Размеры и привязки плана расстановки — в мм от чистовых поверхностей стен: слой штукатурки 20 мм по блоку и 5 мм шпаклёвки по ГКЛ учтён; привязки — от стен и углов помещения, а не от другой мебели.
3. План расстановки не является документацией для изготовления мебели. Встроенная и корпусная мебель изготавливается по чертежам мебельщика после контрольного обмера (после штукатурки); «стена в стену» — с зазором 10 мм с каждой стороны или с компенсаторами; графы «Тип, марка» и «Код продукции» для неё не заполняются (ГОСТ 21.110-2013).
4. Покупные изделия — аналог по характеристикам: заменять только на изделия не больше указанного габарита и того же материала и цвета.
5. Материал и цвет, не указанные в данных изделия, приняты по концепции (лист 18): тон дерева — по полу, обивка — по вторичному цвету палитры; образцы согласовать до заказа.
6. Масса 1 ед. для изделий до 25 кг не указывается. Техника — по монтажным схемам изготовителя; выводы — по листам ЭОМ и ВК.

Допущения и предложения на листе. Знак «**» предложено (согласовать). См. лист открытых вопросов (лист 6).

Изм.	Кол.уч	Лист	№ док.	Подп.	Дата
Разраб.		Кырлан А.С.			04.11.26
Пров.					
ГИП					
Н. контр.					
Утв.					

ГД-2026-009-АИ

Квартира 103 м²

Общая площадь 100,72* м² · * размеры со скана, не замерены (реестр — л. 6, 7, К-1)

Дизайн-проект интерьера

Стадия	Лист	Листов
РП	20	120

Спецификация мебели и оборудования

М б/м

Кырлан Александр Сергеевич

выпуск 04.11.2026 № 20cec94f32 · стр. 22 из 130

Спецификация мебели и оборудования (продолжение)

Форма 1 ГОСТ 21.110-2013 · позиции мебели — по плану расстановки

ПРЕДВАРИТЕЛЬНО · не для производства работ · открыто пунктов: 8 (реестр — л. 6, 7)

Поз.	Наименование и техническая характеристика	Тип, марка, обозначение документа, опросного листа	Код продукции	Поставщик	Ед. измерения	Кол.	Масса 1 ед., кг	Примечание
Кх6	Стол барный у окна, терраццо; Ш×Г×В 700×450×900 мм			аналог по характеристикам	шт.	1		пом. 5; замена ≤ габарита
С1	Кровать 1400×2000, изголовье с каннелюрами, бархат цвета тил; мягкое изголовье, обивка — ткань, цвет Farrow & Ball No. 298; Ш×Г×В 1400×2000×450 мм			аналог по характеристикам	шт.	1		пом. 8; замена ≤ габарита
С3	Туалетный столик середины века с круглым зеркалом; шпон, дуб натуральный, матовое масло; Ш×Г×В 1000×450×750 мм			аналог по характеристикам	шт.	1		пом. 8; замена ≤ габарита
М1	Кровать 1800×2100 с высоким изголовьем ар-деко, изумрудный бархат, латунный кант; мягкое изголовье, обивка ткань, цвет Farrow & Ball No. 298; Ш×Г×В 1800×2100×450 мм			аналог по характеристикам	шт.	1		пом. 10; замена ≤ габарита
М2, М3	Тумба прикроватная, орех и латунь; шпон, дуб натуральный, матовое масло; Ш×Г×В 500×400×550 мм			аналог по характеристикам	шт.	2		пом. 10; замена ≤ габарита
М5	Кресло-лаунж с оттоманкой (в духе Eames Lounge Chair), коньячная кожа; обивка — ткань, цвет Farrow & Ball No. 298; Ш×Г×В 850×850×850 мм			аналог по характеристикам	шт.	1		пом. 10; замена ≤ габарита
М6	Комод ар-деко, макассар и латунь; шпон, дуб натуральный, матовое масло; Ш×Г×В 1400×500×800 мм			аналог по характеристикам	шт.	1		пом. 10; замена ≤ габарита
	Техника встраиваемая и бытовая (покупные изделия), светильники под розетки							
	Посудомоечная машина встраиваемая, в модуле Кх2; ниша 600 мм	аналог по характеристикам: полновстраиваемая 60 см под фасад, ниша 600 × 862 мм, навеска фасада в комплекте		по выбору заказчика до изготовления мебели	шт.	1		пом. 5; по схеме изготовителя
	Духовой шкаф встраиваемый, в модуле Кх4	аналог по характеристикам: 60 см, лицевая панель 595 мм, ниша 560 × 600, глубина ≥ 550 мм, вентиляция за прибором		по выбору заказчика до изготовления мебели	шт.	1		пом. 5; по схеме изготовителя
	Варочная панель встраиваемая, индукционная, в модуле Кх4	аналог по характеристикам: индукционная 60 см, вырез 560 × 490 мм по шаблону модели		по выбору заказчика до изготовления мебели	шт.	1		пом. 5; по схеме изготовителя
	Холодильник встраиваемый, в модуле Кх5	аналог по характеристикам: полновстраиваемый под фасад, ниша 1780 × 560 × 550 мм, вентиляция решётка в цоколе, выход сверху		по выбору заказчика до изготовления мебели	шт.	1		пом. 5; по схеме изготовителя
	Вытяжка, в модуле Кх8**	аналог по характеристикам: производительность — по расчёту ОВ, шум ≤ 55 дБ(А)		по выбору заказчика до изготовления мебели	шт.	1		пом. 5; по схеме изготовителя
	Стиральная машина, место по листу ВК (Пм1); Ш×Г 600×600 мм	аналог по характеристикам: тип загрузки — по листу ВК, в плане 600 × 600 мм (ширина × глубина), по листу ВК		по выбору заказчика до изготовления мебели	шт.	1		пом. 7; по схеме изготовителя
	Торшер, у поз. Г6; абажур — ткань или опаловое стекло; лампа 2700 K			аналог по характеристикам	шт.	1		пом. 3; розетка Р3 (ЭОМ)
	Текстиль							
Т7	Портьеры-волна; лён 100 %; цвет NCS S 1005-Y20R; карниз 1820 мм, высота 2640 мм, сборка 2			аналог по характеристикам	шт.	2		пом. 1
Т8	Тюль; полиэстер 100 %; цвет NCS S 0502-Y; карниз 1820 мм, высота 2640 мм, сборка 2,5			аналог по характеристикам	шт.	1		пом. 1
Т9	Ковёр под рабочей зоной, геометрия середины века; шерсть 100 %; цвет NCS S 2050-Y20R; 2200×1600 мм			аналог по характеристикам	шт.	1		пом. 1; с подложкой
Т10	Подушки декоративные на кровать; букле (шерсть 60 %, полиэстер 40 %); цвет NCS S 3050-Y70R			аналог по характеристикам	шт.	3		пом. 1
Т12	Плед на кровать; шерсть мериноса 100 %; цвет Farrow & Ball No. 289			аналог по характеристикам	шт.	1		пом. 1
Т1	Портьеры-волна, два полотна; лён 100 %; цвет NCS S 1005-Y20R; карниз 2150 мм, высота 2640 мм, сборка 2			аналог по характеристикам	шт.	2		пом. 3
Т2	Тюль-вуаль, одно полотно; полиэстер 100 %; цвет Farrow & Ball No. 291; карниз 2150 мм, высота 2640 мм, сборка 2,5			аналог по характеристикам	шт.	1		пом. 3
Т3	Ковёр мягкой группы, абстрактная геометрия середины века; шерсть 100 %; цвет Farrow & Ball No. 298; 2900×2000 мм			аналог по характеристикам	шт.	1		пом. 3; с подложкой
Т4	Подушки декоративные на диван; лён 100 %; цвет NCS S 1005-Y20R			аналог по характеристикам	шт.	3		пом. 3

Допущения и предложения на листе

Основа листа: размеры сняты со скана обмерного плана KV design (см): часть подписей не читается, помещения выровнены по читаемым размерам; контрольный обмер не выполнен (К-1); высота потолка 2650 мм принята по отметкам обмера (Н = 2,50…2,66 м, ригель 2,28 м) — уточнить при обмере (К-2); толщины стен 300 / 120 мм приняты, межквартирная стена и колонны — по скану, не замерены (К-1); разрешённая мощность 15 кВт принята по типовым ТУ; при объединении двух квартир — переоформление ТУ (К-4); подрайон климата не задан — принят не северный (жилые от 2,5 м) (К-8).

Знак «**» — предложение проектировщика, заказчиком не утверждено (согласовать с заказчиком): Кх8 — над индукционной панелью Кх4 нужна вытяжка: в составе кухни её не было, розетка вытяжки образца висела без потребителя.

См. лист открытых вопросов (лист 6, записи К-1, К-2, К-4, К-8).

Изм.	Кол.уч	Лист	№ док.	Подп.	Дата
Разраб.		Кырлан А.С.			04.11.26
Пров.					
ГИП					
Н. контр.					
Утв.					

ГД-2026-009-АИ

Квартира 103 м²

Общая площадь 100,72* м² · * размеры со скана, не замерены (реестр — л. 6, 7, К-1)

Дизайн-проект интерьера	Стадия	Лист	Листов
	РП	21	120
Спецификация мебели и оборудования (продолжение) М б/м	**Кырлан Александр Сергеевич**		

Спецификация мебели и оборудования (продолжение)

Форма 1 ГОСТ 21.110-2013 · позиции мебели — по плану расстановки

ПРЕДВАРИТЕЛЬНО · не для производства работ · открыто пунктов: 8 (реестр — л. 6, 7)

Поз.	Наименование и техническая характеристика	Тип, марка, обозначение документа, опросного листа	Код продукции	Поставщик	Ед. измерения	Кол.	Масса 1 ед., кг	Примечание
Т5	Подушки декоративные на диван, акцент; хлопковый бархат 100 %; цвет Farrow & Ball No. 255			аналог по характеристикам	шт.	2		пом. 3
Т6	Плед на диван; шерсть мериноса 100 %; цвет Farrow & Ball No. 255			аналог по характеристикам	шт.	1		пом. 3
Т14	Рулонная штора кассетная, ткань димаут; полиэстер 100 %; цвет NCS S 1005-Y20R; карниз 1600 мм, высота 1750 мм			аналог по характеристикам	шт.	1		пом. 5
Т11	Портьеры-волна; лён 100 %; цвет NCS S 1005-Y20R; карниз 1820 мм, высота 2640 мм, сборка 2			аналог по характеристикам	шт.	2		пом. 8
Т13	Тюль; полиэстер 100 %; цвет NCS S 0502-Y; карниз 1820 мм, высота 2640 мм, сборка 2,5			аналог по характеристикам	шт.	1		пом. 8
Т15	Ковёр под кроватью; шерсть 100 %; цвет NCS S 2050-Y20R; 2300×1500 мм			аналог по характеристикам	шт.	1		пом. 8; с подложкой
Т16	Подушки декоративные на кровать; букле (шерсть 60 %, полиэстер 40 %); цвет NCS S 3050-Y70R			аналог по характеристикам	шт.	3		пом. 8
Т17	Подушки на кровать, акцент; хлопковый бархат 100 %; цвет NCS S 5030-B10G			аналог по характеристикам	шт.	2		пом. 8
Т18	Плед на кровать; шерсть мериноса 100 %; цвет Farrow & Ball No. 289			аналог по характеристикам	шт.	1		пом. 8
Т19	Портьеры-волна; лён 100 %; цвет NCS S 1005-Y20R; карниз 2500 мм, высота 2640 мм, сборка 2			аналог по характеристикам	шт.	2		пом. 10
Т20	Тюль; полиэстер 100 %; цвет NCS S 0502-Y; карниз 2500 мм, высота 2640 мм, сборка 2,5			аналог по характеристикам	шт.	1		пом. 10
Т21	Ковёр под кроватью; шерсть 80 %, хлопок 20 %; цвет Farrow & Ball No. 298; 2800×1850 мм			аналог по характеристикам	шт.	1		пом. 10; с подложкой
Т22	Подушки декоративные на кровать; лён 100 %; цвет NCS S 1005-Y20R			аналог по характеристикам	шт.	3		пом. 10
Т23	Подушки на кровать, акцент; хлопковый бархат 100 %; цвет Farrow & Ball No. 289			аналог по характеристикам	шт.	2		пом. 10
Т24	Плед на кровать; шерсть мериноса 100 %; цвет Farrow & Ball No. 289			аналог по характеристикам	шт.	1		пом. 10
	Декор							
ДК3	Картина над креслом: графика середины века, рама — орех; 1000×700 мм; низ на 1100 мм от пола			аналог по характеристикам	шт.	1	4	пом. 1; крепление к стене
ДК1	Картина над буфетом: абстракция середины века, рама — латунь; 1200×900 мм; низ на 1000 мм от пола			аналог по характеристикам	шт.	1	6	пом. 3; крепление: планка на дюбелях, 4 точки
ДК2	Фикус лировидный в кашпо Ø400; 450×450 мм			аналог по характеристикам	шт.	1		пом. 3
ДК5	Зеркало; рама — чёрный матовый; 800×1800 мм; низ на 550 мм от пола			аналог по характеристикам	шт.	1	18	пом. 4; крепление: анкер, 4 шт.
ДК8	Часы настенные Ø400; 400×400 мм; центр на 1550 мм от пола			аналог по характеристикам	шт.	1	2	пом. 5; крепление: дюбель с крюком, 1 точка
ДК9	Хлорофитум хохлатый на подоконнике (отм. +0,800); 300×200 мм; низ на 800 мм от пола			аналог по характеристикам	шт.	1		пом. 5
ДК4	Картина над кроватью: графика в паспарту, рама — дуб; 1000×700 мм; низ на 1100 мм от пола			аналог по характеристикам	шт.	1	4	пом. 8; крепление к стене
ДК6	Зеркало в рост в тонкой чёрной раме; рама — чёрный матовый; 600×1600 мм; низ на 300 мм от пола			аналог по характеристикам	шт.	1	12	пом. 8; крепление: анкер для пустотелых оснований, 4 шт.
ДК7	Картина над кроватью: абстракция, холст, тонкая рама из дуба; 1200×700 мм; низ на 1300 мм от пола			аналог по характеристикам	шт.	1	4	пом. 10; крепление к стене

Допущения и предложения на листе

Основа листа: размеры сняты со скана обмерного плана KV design (см): часть подписей не читается, помещения выровнены по читаемым размерам; контрольный обмер не выполнен (К-1); высота потолка 2650 мм принята по отметкам обмера (Н = 2,50…2,66 м, ригель 2,28 м) — уточнить при обмере (К-2); толщины стен 300 / 120 мм приняты, межквартирная стена и колонны — по скану, не замерены (К-1); разрешённая мощность 15 кВт принята по типовым ТУ; при объединении двух квартир — переоформление ТУ (К-4); подрайон климата не задан — принят не северный (жилые от 2,5 м) (К-8).

См. лист открытых вопросов (лист 6, записи К-1, К-2, К-4, К-8).

Изм.	Кол.уч	Лист	№ док.	Подп.	Дата
Разраб.		Кырлан А.С.			04.11.26
Пров.					
ГИП					
Н. контр.					
Утв.					

ГД-2026-009-АИ

Квартира 103 м²

Общая площадь 100,72* м² · * размеры со скана, не замерены (реестр — л. 6, 7, К-1)

Дизайн-проект интерьера

Стадия	Лист	Листов
РП	22	120

Спецификация мебели и оборудования (продолжение)

М б/м

Кырлан Александр Сергеевич

03

Электрооборудование


Кырлан Александр Сергеевич

выпуск 04.11.2026 № 20cec94f32 · стр. 25 из 130

План розеток и электровыводов

Розетки, выводы кабеля, щит · размеры в мм · высоты от чистого пола

ПРЕДВАРИТЕЛЬНО · не для производства работ · открыто пунктов: 8 (реестр — л. 6, 7)

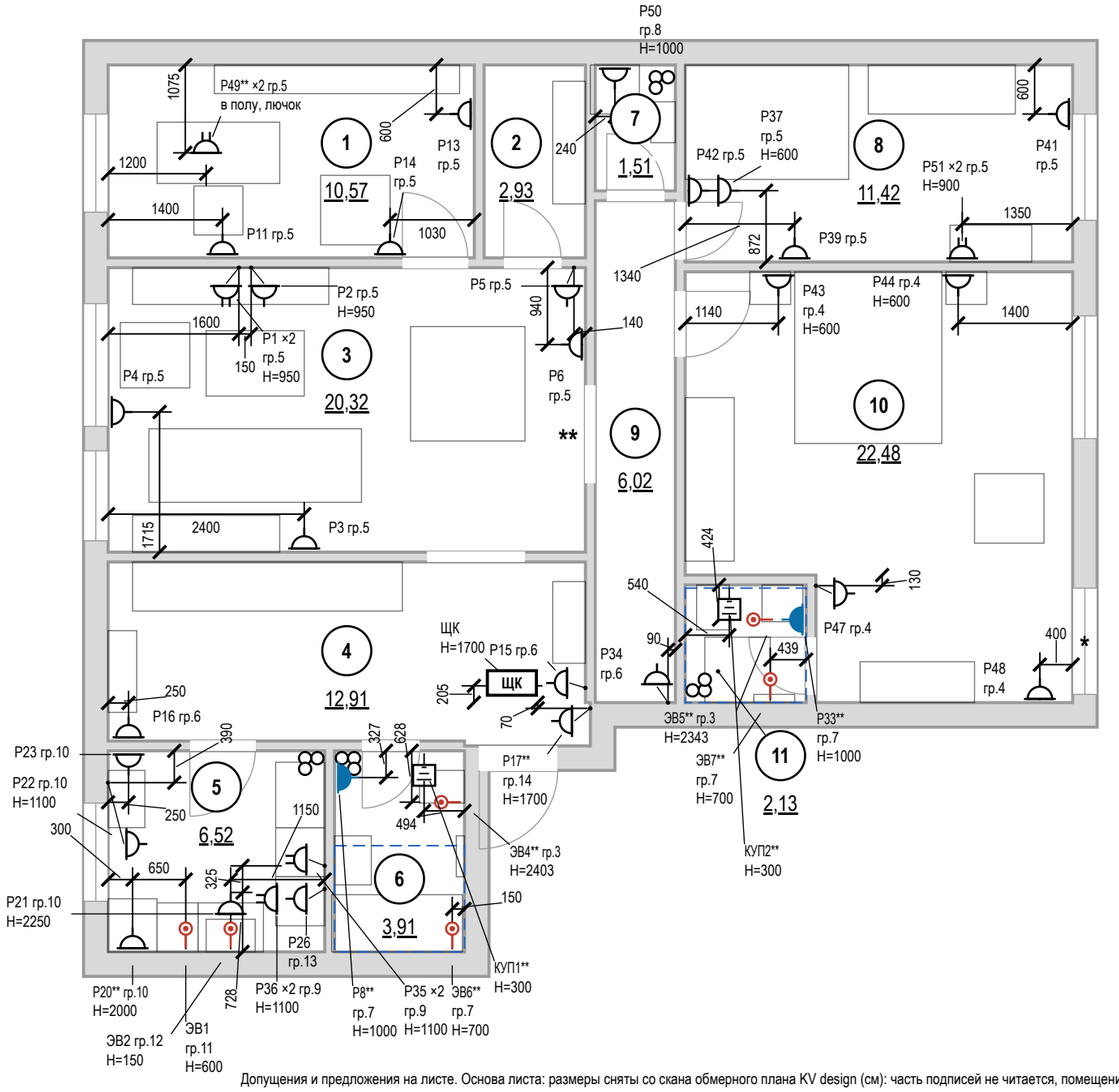

Условные обозначения

Знак	Тип изделия	H, мм	Кол., шт
	Розетка с заземлением	300	17
	То же	у знака	9
	Блок розеток с заземлением, рамка 2 поста	у знака	5
	Розетка с заземлением IP44	1000	2
	Вывод кабеля к прибору	у знака	6
	КУП (уравнивание потенциалов)	300	2
ЩК	Щит квартирный	1700	1

розетка с заземляющим контактом; у знака — марка, ×N — постов в рамке, гр. — группа щита, H — высота оси, мм

знак разведён для читаемости: точка на стене — у выноски, привязка — до неё

граница зоны 2 ванной (600 мм от ванны/поддона)

мебель и сантехприборы — подложка

стояк: К1 — канализация, В1 — ХВС, Т3 — ГВС

1 — номер помещения, площадь м²

Итого розеток (механизмов) — 38 шт; рамок — 33 шт: на 1 пост — 28, на 2 поста — 5.

Допущения и предложения на листе. Основа листа: размеры сняты со скана обмерного плана KV design (см): часть подписей не читается, помещения выровнены по читаемым размерам; контрольный обмер не выполнен (К-1); высота потолка 2650 мм принята по отметкам обмера (H = 2,50…2,66 м, ригель 2,28 м) — уточнить при обмере (К-2); толщины стен 300 / 120 мм приняты, межквартирная стена и колонны — по скану, не замерены (К-1); разрешённая мощность 15 кВт принята по типовым ТУ; при объединении двух квартир — переоформление ТУ (К-4); подрайон климата не задан — принят не северный (жилые от 2,5 м) (К-8). Знак «*» — принято, не замерено (замерить): К-6: Ст К1-3, Ст В1-3, Ст Т3-3. Знак «**» — предложено, не утверждено (согласовать): P49, P17, P20, КУП1, ЭВ5, КУП2; ИЗ-1: P8, ЭВ4, ЭВ6, P33, ЭВ7. См. лист открытых вопросов (лист 6, записи ИЗ-1, К-1, К-2, К-4–К-6, К-8).

Примечания

1. За отметку 0,000 принят уровень чистого пола. Высоты H — от чистого пола до оси изделия; привязки — от чистовой грани стены до оси механизма (у рамки на несколько постов — до оси рамки).
2. Розетки без отметки H у знака — на высоте 300 мм от чистого пола до оси механизма; выводы кабеля — по паспорту прибора.
3. Розетки в санузле — только вне зон 0–2 (ПУЭ 7.1.48, ГОСТ Р 50571.7.701-2024), IP44, через УЗО 30 мА.
4. Розеточные и мокрые линии — через УЗО или дифавтомат с током утечки не более 30 мА (ПУЭ 7.1.79); в санузле выполнить ДСУП (ПУЭ 7.1.87–7.1.88).
5. Кабель — медный, исполнение нг(A)-LS (ГОСТ 31565-2012); скрытая прокладка только горизонтально и вертикально, фактические трассы зафиксировать исполнительной схемой до закрытия отделкой.
6. Расчёт нагрузок, токов КЗ, селективности и сечений — по проекту ЭОМ организации с допуском СРО; лист задаёт состав, расположение и группы.
7. Выводы кухонной техники — после утверждения проекта кухни (ориентировочно); привязки выводов даны от осей модулей гарнитура и пересматриваются вместе с проектом кухни.
8. Электрический тёплый пол проектом не предусмотрен; при решении заказчика устроить — отдельный лист «План тёплых полов»: контуры с отступом 100 мм от стен и мебели без ножек, датчик в гофре, терморегулятор, своя группа щита через УЗО 30 мА.
9. Ведомости электроточек, изделий, светильников и расшифровка клавиш — лист 26.

1000 мм · печать 1:1

Изм.	Кол.уч	Лист	№ док.	Подп.	Дата
Разраб.		Кырлан А.С.			04.11.26
Пров.					
ГИП					
Н. контр.					
Утв.					

ГД-2026-009-АИ

Квартира 103 м²

Общая площадь 100,72* м² · * размеры со скана, не замерены (реестр — л. 6, 7, К-1)

Дизайн-проект интерьера

Стадия	Лист	Листов
РП	23	120

План розеток и электровыводов


М 1:75

Кырлан Александр Сергеевич

выпуск 04.11.2026 № 20cec94f32 · стр. 26 из 130

План освещения

Светильники, группы включения, извещатели · размеры в мм

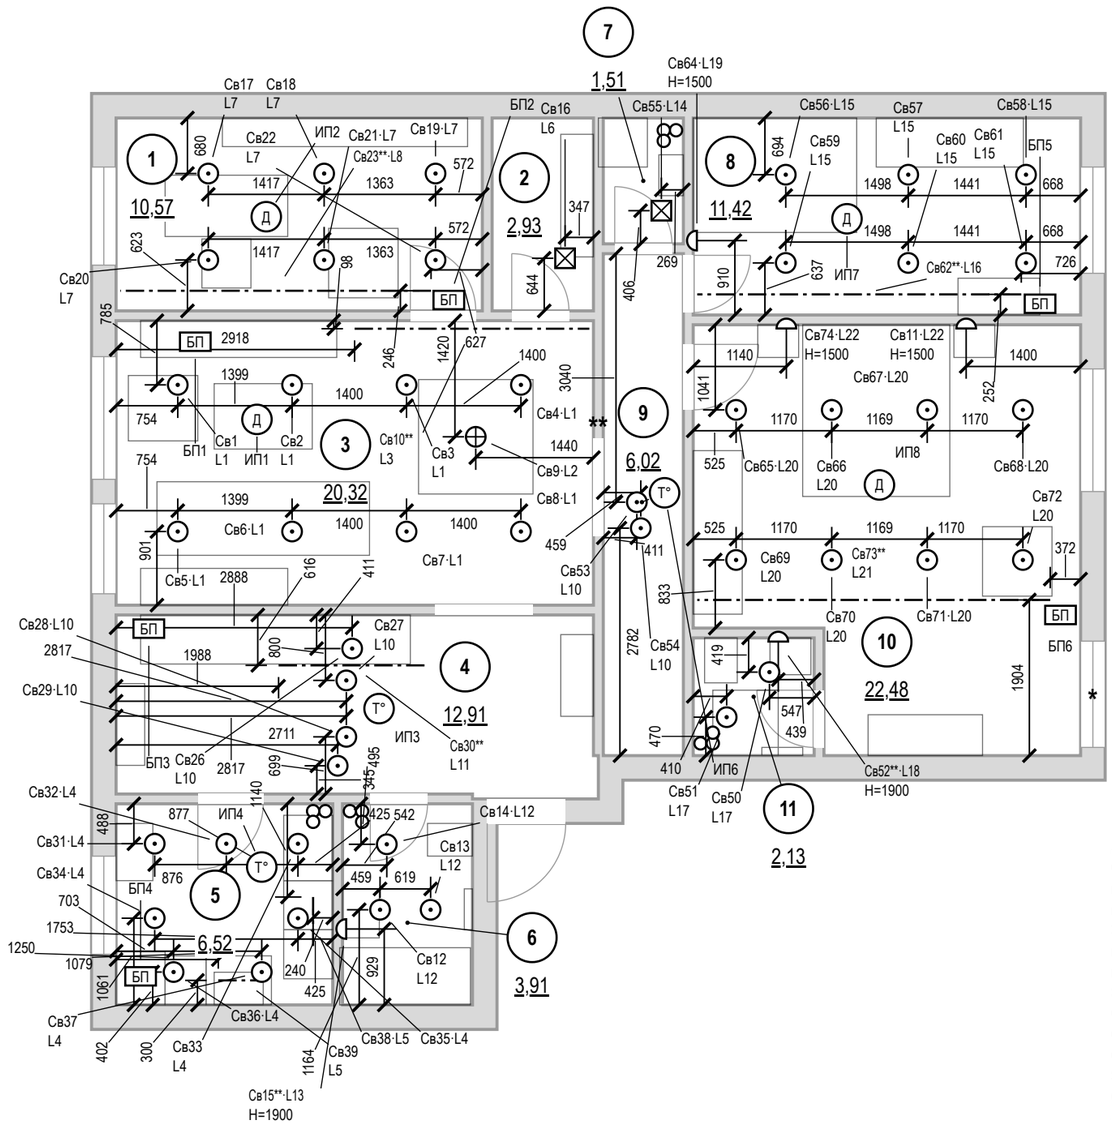

Условные обозначения

- светильник встраиваемый точечный
- светильник потолочный накладной
- светильник подвесной
- светильник настенный (бра), H — высота оси
- светодиодная лента в профиле / в карнизе короба
- Св1·L1 — марка светильника (как в ведомости и на развёртках) · группа включения L (лист 25)
- Д — извещатель пожарный дымовой автономный
- T° — извещатель пожарный тепловой
- БП — блок питания LED, с доступом (люк от 100×100 мм)
- мебель и сантехприборы — подложка
- стояк: К1 — канализация, В1 — ХВС, Т3 — ГВС
- 1 — номер помещения, площадь м²

Допущения и предложения на листе

Основа листа: размеры сняты со скана обмерного плана KV design (см): часть подписей не читается, помещения выровнены по читаемым размерам; контрольный обмер не выполнен (К-1); высота потолка 2650 мм принята по отметкам обмера (H = 2,50…2,66 м, ригель 2,28 м) — уточнить при обмере (К-2); толщины стен 300 / 120 мм приняты, межквартирная стена и колонны — по скану, не замерены (К-1); разрешённая мощность 15 кВт принята по типовым ТУ; при объединении двух квартир — переоформление ТУ (К-4); подрайон климата не задан — принят не северный (жилые от 2,5 м) (К-8).

Знак «*» — принято, не замерено и не подтверждено (замерить на объекте): К-1: окно пом. 10 (стена Б) — Окно 1300 при offset 3500 на стене Б основной части (длина 3830) выходило за стену на 970 мм; К-6: Ст К1-3, Ст В1-3, Ст Т3-3 — положение снято со скана обмера, отдельно не замерялось; ось внутри габарита поддона См1 — обмер угла по К-6.

Знак «**» — предложение проектировщика, заказчиком не утверждено (согласовать с заказчиком): Св23, Св10, Св30, Св62, Св73 — открытая лента в накладном профиле вместо «в коробе»: короба в потолке нет — высота 2650 мм < 2700 — один уровень (табл. 1.3); Св15 — Сдвиг под раскладку плитки стены Г на 141 мм вдоль стены — ось на шве или в центре плитки, привязка по таблице листа; Св52 — свет у зеркала — над зеркалом у умывальника по его оси (свет на лицо, а не над сантехникой); сдвиг под раскладку плитки стены А на 149 мм вдоль стены — ось на шве или в центре плитки, привязка по таблице листа; К-5: дверь пом. 3 (стена Б) — проём в межквартирной стене — объединение квартир, предложение до техзаключения. См. лист открытых вопросов (лист 6, записи К-1, К-2, К-4–К-6, К-8).

Примечания

1. За отметку 0,000 принят уровень чистого пола. Высоты H — от чистого пола до оси изделия; привязки — от чистовой грани стены до оси механизма (у рамки на несколько постов — до оси рамки).
2. Высота установки, не указанная на плане: светильники — на потолке; настенные — по отметке H у знака. Привязки — до оси светильника от чистовой грани стены, по рядам.
3. Во влажных помещениях — светильники не ниже IP44; в зонах 0–2 ванной — по ГОСТ Р 50571.7.701-2024 (зона 1 — IPX5).
4. Розеточные и мокрые линии — через УЗО или дифавтомат с током утечки не более 30 мА (ПУЭ 7.1.79); в санузле выполнить ДСУП (ПУЭ 7.1.87–7.1.88).
5. Кабель — медный, исполнение нг(A)-LS (ГОСТ 31565-2012); скрытая прокладка только горизонтально и вертикально, фактические трассы зафиксировать исполнительной схемой до закрытия отделкой.
6. Расчёт нагрузок, токов КЗ, селективности и сечений — по проекту ЭОМ организации с допуском СРО; лист задаёт состав, расположение и группы.
7. Ведомость светильников (тип, количество, мощность, поток, Tц, Ra) — лист 43.
8. Оценка освещённости (по норме СанПиН 1.2.3685-21, табл. 5.52, на полу; не светотехнический расчёт, декоративная подсветка в оценку не входит) — лист 26.

1000 мм · печать 1:1

Изм.	Кол.уч	Лист	№ док.	Подп.	Дата
Разраб.		Кырлан А.С.			04.11.26
Пров.					
ГИП					
Н. контр.					
Утв.					

ГД-2026-009-АИ

Квартира 103 м²

Общая площадь 100,72* м² · * размеры со скана, не замерены (реестр — л. 6, 7, К-1)

Дизайн-проект интерьера

Стадия	Лист	Листов
РП	24	120

План освещения

М 1:75


Кырлан Александр Сергеевич

выпуск 04.11.2026 № 20cec94f32 · стр. 27 из 130

План выключателей и схема включения

Выключатели S, группы включения L, линии связи · размеры в мм

ПРЕДВАРИТЕЛЬНО · не для производства работ · открыто пунктов: 8 (реестр — л. 6, 7)

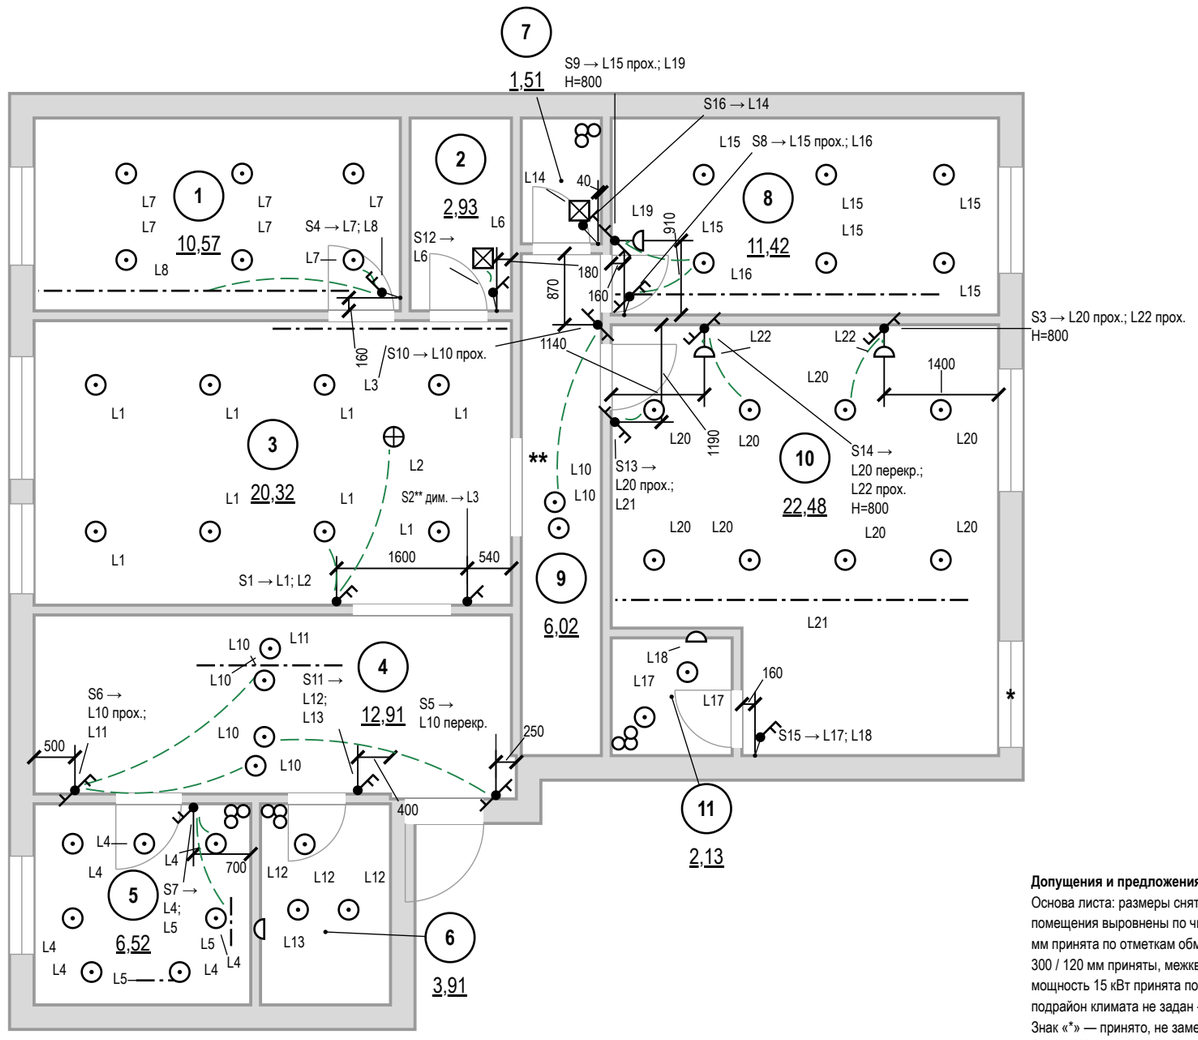

Условные обозначения

- выключатель одноклавишный
- выключатель двухклавишный (флажков — по числу клавиш)
- выключатель с проходной или перекрёстной клавишей (обратный флажок); тип клавиши — в подписи
- S1 → — марка → группы по клавишам (через «;»): прох. — проходной, перекр. — перекрёстный, дим. — светорегулятор; Н — высота
- связь: выключатель → ближайший светильник группы в том же помещении (не трасса кабеля); полный состав группы — по номеру L
- светильник встраиваемый точечный
- светильник потолочный накладной
- светильник подвесной
- светильник настенный (бра), Н — высота оси
- светодиодная лента в профиле / в карнизе короба
- L1 — группа включения у светильника
- стояк: К1 — канализация, В1 — ХВС, Т3 — ГВС
- 1 — номер помещения, площадь м²

Допущения и предложения на листе

Основа листа: размеры сняты со скана обмерного плана KV design (см): часть подписей не читается, помещения выровнены по читаемым размерам; контрольный обмер не выполнен (К-1); высота потолка 2650 мм принята по отметкам обмера (Н = 2,50…2,66 м, ригель 2,28 м) — уточнить при обмере (К-2); толщины стен 300 / 120 мм приняты, межквартирная стена и колонны — по скану, не замерены (К-1); разрешённая мощность 15 кВт принята по типовым ТУ; при объединении двух квартир — переоформление ТУ (К-4); подрайон климата не задан — принят не северный (жилые от 2,5 м) (К-8).

Знак «*» — принято, не замерено и не подтверждено (замерить на объекте): К-1: окно пом. 10 (стена Б) — Окно 1300 при offset 3500 на стене Б основной части (длина 3830) выходило за стену на 970 мм; К-6: Ст К1-3, Ст В1-3, Ст Т3-3 — положение снято со скана обмера, отдельно не замерялось; ось внутри габарита поддона См1 — обмер угла по К-6.

Знак «**» — предложение проектировщика, заказчиком не утверждено (согласовать с заказчиком): S2 — светорегулятор добавлен под диммируемую ленту L3; уровни сценариев выбраны конвейером; К-5: дверь пом. 3 (стена Б) — проём в межквартирной стене — объединение квартир, предложение до техзаключения. См. лист открытых вопросов (лист 6, записи К-1, К-2, К-4–К-6, К-8).

Примечания

1. За отметку 0,000 принят уровень чистого пола. Высоты Н — от чистого пола до оси изделия; привязки — от чистовой грани стены до оси механизма (у рамки на несколько постов — до оси рамки).
2. Высота установки, не указанная на плане: выключатели — 900 мм от чистого пола (у кровати и другие — Н у марки), со стороны дверной ручки (ПУЭ 7.1.51).
3. Какой выключатель какие светильники включает — по номеру группы L: у выключателя (S1 → L1; L2 — клавиши по порядку) и у каждого светильника. Пунктир подсказка к ближайшему светильнику группы в том же помещении (не дальше 3 м), это не трасса кабеля; выключатель за стеной (у двери санузла) и далёкая группа — только номер группы.
4. Группы из нескольких мест (L10 — S5, S6, S10; L15 — S8, S9; L20 — S3, S13, S14; L22 — S3, S14): на крайних местах — проходные клавиши, на промежуточных перекрёстные; механизмы — в ведомости изделий.
5. Светорегулятор — по заднему фронту (для LED-драйверов), совместимость с драйверами проверить до закупки.
6. Розеточные и мокрые линии — через УЗО или дифавтомат с током утечки не более 30 мА (ПУЭ 7.1.79); в санузле выполнить ДСУП (ПУЭ 7.1.87–7.1.88).
7. Кабель — медный, исполнение нг(А)-LS (ГОСТ 31565-2012); скрытая прокладка только горизонтально и вертикально, фактические трассы зафиксировать исполнительной схемой до закрытия отделкой.
8. Расчёт нагрузок, токов КЗ, селективности и сечений — по проекту ЭОМ организации с допуском СРО; лист задаёт состав, расположение и группы.
9. Расшифровка клавиш и ведомость изделий — лист 26.

1000 мм · печать 1:1

Изм.	Кол.уч	Лист	№ док.	Подп.	Дата
Разраб.		Кырлан А.С.			04.11.26
Пров.					
ГИП					
Н. контр.					
Утв.					

ГД-2026-009-АИ

Квартира 103 м²

Общая площадь 100,72* м² · * размеры со скана, не замерены (реестр — л. 6, 7, К-1)

Дизайн-проект интерьера

Стадия	Лист	Листов
РП	25	120

План выключателей и схема включения

М 1:75

Кырлан Александр Сергеевич

выпуск 04.11.2026 № 20cec94f32 · стр. 28 из 130

Ведомость электроточек и изделий

Электроточки, изделия, светильники, освещённость, клавиши выключателей · б/м

Ведомость электроточек

Марка	Пом.	Назначение	H, мм	Гр.
Р11	1	общего назначения	300	5
Р13	1	уборка	300	5
Р14	1	уборка у входа	300	5
Р49**	1	рабочий стол — лючок в полу под столом	0	5
Р1	3	ТВ-зона: телевизор, медиаплеер	950	5
Р2	3	ТВ-зона: саундбар	950	5
Р3	3	торшер у дивана Г2	300	5
Р4	3	кресло у окна Г4	300	5
Р5	3	обеденная зона, буфет Г6	300	5
Р6	3	уборка	300	5
Р15	4	пылесос, сушилка обуви	300	6
Р16	4	уборка	300	6
Р17**	4	питание слаботочного щита (рядом с ЩС**)	1700	14
ЩК	4	щит квартирный ЩРВ-П-48	1700	
Р20**	5	холодильник — над нишей, съёмная панель	2000	10
Р21	5	вытяжка — над корпусом	2250	10
Р22	5	барный стол Кх6: мелкая техника	1100	10
Р23	5	уборка	300	10
Р26	5	посудомоечная машина — в соседнем модуле, за ящиком	300	13
Р35	5	фартук	1100	9
Р36	5	фартук	1100	9
ЭВ1	5	варочная панель — в соседнем модуле, за ящиком	600	11
ЭВ2	5	духовой шкаф — в цоколе	150	12
КУП1**	6	КУП — уравнивание потенциалов (ДСУП)	300	
Р8**	6	фен у умывальника, IP44	1000	7
ЭВ4**	6	вентилятор ВР1 (таймер выбега)	2403	3
ЭВ6**	6	полотенцесушитель П10, IP44	700	7
Р50	7	стиральная машина	1000	8
Р37	8	у кровати	600	5
Р39	8	общего назначения	300	5

Ведомость электроточек (продолжение)

Марка	Пом.	Назначение	H, мм	Гр.
Р41	8	уборка	300	5
Р42	8	уборка у входа	300	5
Р51	8	туалетный столик: фен, подсветка зеркала	900	5
Р34	9	уборка	300	6
Р43	10	у кровати	600	4
Р44	10	у кровати	600	4
Р47	10	общего назначения	300	4
Р48	10	уборка	300	4
КУП2**	11	КУП — уравнивание потенциалов (ДСУП)	300	
Р33**	11	фен у умывальника, IP44	1000	7
ЭВ5**	11	вентилятор ВР3 (таймер выбега)	2343	3
ЭВ7**	11	полотенцесушитель П13, IP44	700	7

Ведомость изделий

Наименование	Марки	Ед.	Кол.
Розетка с з/к и защитными шторками, 16 А	по ведомости точек	шт	36
Розетка IP44 с крышкой, 16 А	Р8**, Р33**	шт	2
Выключатель 1-клав.	S12, S16	шт	2
Выключатель 1-клав. перекрёстный	S5	шт	1
Выключатель 1-клав. проходной	S10	шт	1
Выключатель 2-клав.	S1, S4, S7, S11, S15	шт	5
Выключатель 2-клав. (перекрёстная + проходная)	S14	шт	1
Выключатель 2-клав. (проходная + обычная)	S6, S8, S9, S13	шт	4
Выключатель 2-клав. проходной	S3	шт	1
Светорегулятор 1-канальный, задний фронт (LED)	S2**	шт	1
Датчик движения ночной подсветки	L11	шт	1
Рамка 1-постовая	в т. ч. 16 под выключ.	шт	44
Рамка 2-постовая		шт	5
Коробка установочная (подрозетник) Ø68	розетки, выключатели	шт	54

Ведомость изделий (продолжение)

Наименование	Марки	Ед.	Кол.
Вывод кабеля под прибор (клеммник)	ЭВ1, ЭВ2, ЭВ4**, ЭВ5**, ЭВ6**, ЭВ7**	шт	6
Коробка уравнивания потенциалов КУП	КУП1**, КУП2**	шт	2
Блок питания LED 24 В, 200 Вт, дим.	БП2, БП5, БП6	шт	3
Блок питания LED 24 В, 100 Вт, дим.	БП1	шт	1
Блок питания LED 24 В, 20 Вт	БП3	шт	1
Блок питания LED 24 В, 30 Вт	БП4	шт	1
Извещатель дымовой автономный	ИП1, ИП2, ИП7, ИП8	шт	4
Извещатель тепловой	ИП3, ИП4, ИП6	шт	3
Щит квартирный (состав — лист щита)	ЩК	шт	1
Розетка компьютерная RJ45, кат. 6, с рамкой и подрозетником	LAN1, LAN3, LAN4, LAN5**	шт	4
Розетка телевизионная (коаксиальная) с рамкой и подрозетником	ТВ1	шт	1
Точка доступа Wi-Fi (оборудование заказчика), питание PoE	АР1**	шт	1
Трубка или монитор домофона (поставка домофонной организации)	ДФ1	шт	1
Щит слаботочный ЩС**: корпус, DIN-рейка, розетки 220 В	ЩС**	шт	1
Патч-панель, портов не менее 5		шт	1
Коммутатор, портов не менее 5, из них PoE 1		шт	1
Кабель домофона — тип по системе поставщика (по лучам от ЩС**, запас 10 %)		м	4,3
Кабель коаксиальный RG-6 (75 Ом) к розеткам ТВ (по лучам от ЩС**, запас 10 %)		м	16,1
Кабель U/UTP кат. 6 (LAN, Wi-Fi и камеры по PoE) (по лучам от ЩС**, запас 10 %)		м	70,3

Допущения и предложения на листе. Основа листа: размеры сняты со скана обмерного плана KV design (см): часть подписей не читается, помещения выровнены по читаемым размерам; контрольный обмер не выполнен (К-1); высота потолка 2650 мм принята по отметкам обмера (Н = 2,50…2,66 м, ригель 2,28 м) — уточнить при обмере (К-2); толщины стен 300 / 120 мм приняты, межквартирная стена и колонны — по скану, не замерены (К-1); разрешённая мощность 15 кВт принята по типовым ТУ; при объединении двух квартир — переоформление ТУ (К-4); подрайон климата не задан — принят не северный (жилые от 2,5 м) (К-8). Знак «**» — предложено, не утверждено (согласовать): Св23, Р49, LAN5, S2, Св10, Р17, Св30, Р20, Св15, КУП1, Св62, Св73, Св52, ЭВ5, КУП2, ЩС, АР1; ИЗ-1: Р8, ЭВ4, ЭВ6, Р33, ЭВ7. См. лист открытых вопросов (лист 6, записи ИЗ-1, К-1, К-2, К-4, К-8).

Ведомость светильников

Поз.	Марки	Тип	Кол.	P, Вт	Ф, лм	IP	Тц/Ra
1	Св17–Св22, Св56–Св61	встраиваемый точечный	12	12	1050		2700/90
2	Св23**, Св62**	светодиодная лента, 12,3 м	2	118,1	11070		2700/90
3	Св16, Св55	потолочный накладной	2	10	900		3000/90
4	Св1–Св8, Св31–Св37	встраиваемый точечный	15	12	1000		3000/90
5	Св9	подвесной	1	15	1200		2700/90
6	Св10**	светодиодная лента, 5,4 м	1	51,8	4860		2700/90
7	Св26–Св29, Св53, Св54	встраиваемый точечный	6	7	600		3000/90
8	Св30**	светодиодная лента, 1,8 м	1	8,6	270		2700/90
9	Св38, Св39	линейный светильник	2	8	700		3000/90
10	Св12–Св14, Св51	встраиваемый точечный	4	6	500	44	3000/90
11	Св15**, Св52**	настенный (бра), H=1900	2	8	600	44	3000/90
12	Св11, Св64, Св74	настенный (бра), H=1500	3	6	400		2700/90
13	Св65–Св72	встраиваемый точечный	8	12	1000		2700/90
14	Св73**	светодиодная лента, 15,5 м	1	148,8	13950		2700/90
15	Св50	встраиваемый точечный	1	7	600	44	3000/90

Освещённость (оценка)

Пом.	S, м²	Ен, лк	Ф треб., лм	Ф по пр., лм
1	10,6	300	8930	6300
2	2,9	30	250	900
3	20,3	150	8590	8000
4	12,9	50	1820	2400
5	6,5	150	2750	7000
6	3,9	50	550	1500
7	1,5	75	320	900
8	11,4	150	4830	6300

Примечания

1. Ведомости сведены с планов розеток, освещения и выключателей; марки, группы и высоты — те же, что у знаков на планах.
2. Механизмы, рамки и светорегуляторы — одной серии; число постов и клавиш сверено с выбранной серией. Перекрёстная клавиша — отдельный механизм серии.
3. Освещённость (оценка) — по норме СанПиН 1.2.3685-21 (табл. 5.52, на полу), не светотехнический расчёт; декоративная подсветка в оценку не входит.
4. За отметку 0,000 принят уровень чистого пола. Высоты Н — от чистого пола до оси изделия; привязки — от чистовой грани стены до оси механизма (у рамки на несколько постов — до оси рамки).
5. Розеточные и мокрые линии — через УЗО или дифавтомат с током утечки не более 30 мА (ПУЭ 7.1.79); в санузле выполнить ДСУП (ПУЭ 7.1.87–7.1.88).
6. Кабель — медный, исполнение нг(А)-LS (ГОСТ 31565-2012); скрытая прокладка только горизонтально и вертикально, фактические трассы зафиксировать исполнительной схемой до закрытия отделкой.
7. Расчёт нагрузок, токов КЗ, селективности и сечений — по проекту ЭОМ организации с допуском СРО; лист задаёт состав, расположение и группы.
8. Ведомости занимают 2 листов этого наименования: таблицы, не вошедшие в поле листа, продолжены на следующем листе.

Изм.	Кол.уч	Лист	№ док.	Подп.	Дата
Разраб.		Кырлан А.С.			04.11.26
Пров.					
ГИП					
Н. контр.					
Утв.					

ГД-2026-009-АИ

Квартира 103 м²

Общая площадь 100,72* м² · * размеры со скана, не замерены (реестр — л. 6, 7, К-1)

Дизайн-проект интерьера

Стадия	Лист	Листов
РП	26	120

Ведомость электроточек и изделий

М б/м

Кырлан Александр Сергеевич

выпуск 04.11.2026 № 20cec94f32 · стр. 29 из 130

Ведомость электроточек и изделий (продолжение)

Электроточки, изделия, светильники, освещённость, клавиши выключателей · б/м

Освещённость (оценка) (продолжение)

Пом.	S, м²	Ен, лк	Ф треб., лм	Ф по пр., лм
9	6	50	850	1200
10	22,5	150	9500	8000
11	2,1	50	300	1100

Расшифровка клавиш

Марка	Пом.	H, мм	Клав.	Механизм	Группа: светильники
S1	3	900	1	обычный	L1: Св1–Св8
			2	обычный	L2: Св9
S2**	3	900	1	светорегулятор	L3: Св10**
S3	10	800	1	проходной	L20: Св65–Св72
			2	проходной	L22: Св11, Св74
S4	1	900	1	обычный	L7: Св17–Св22
			2	обычный	L8: Св23**
S5	4	900	1	перекрёстный	L10: Св26–Св29, Св53, Св54
S6	4	900	1	проходной	L10: Св26–Св29, Св53, Св54
			2	обычный	L11: Св30**
S7	5	900	1	обычный	L4: Св31–Св37
			2	обычный	L5: Св38, Св39
S8	8	900	1	проходной	L15: Св56–Св61
			2	обычный	L16: Св62**
S9	8	800	1	проходной	L15: Св56–Св61
			2	обычный	L19: Св64
S10	9	900	1	проходной	L10: Св26–Св29, Св53, Св54
S11	4	900	1	обычный	L12: Св12–Св14
			2	обычный	L13: Св15**
S12	2	900	1	обычный	L6: Св16
S13	10	900	1	проходной	L20: Св65–Св72
			2	обычный	L21: Св73**
S14	10	800	1	перекрёстный	L20: Св65–Св72
			2	проходной	L22: Св11, Св74
S15	10	900	1	обычный	L17: Св50, Св51
			2	обычный	L18: Св52**
S16	7	900	1	обычный	L14: Св55

Допущения и предложения на листе

Основа листа: размеры сняты со скана обмерного плана KV design (см): часть подписей не читается, помещения выровнены по читаемым размерам; контрольный обмер не выполнен (К-1); высота потолка 2650 мм принята по отметкам обмера (H = 2,50…2,66 м, ригель 2,28 м) — уточнить при обмере (К-2); толщины стен 300 / 120 мм приняты, межквартирная стена и колонны — по скану, не замерены (К-1); разрешённая мощность 15 кВт принята по типовым ТУ; при объединении двух квартир — переоформление ТУ (К-4); подрайон климата не задан — принят не северный (жилые от 2,5 м) (К-8).

Знак «**» — предложение проектировщика, заказчиком не утверждено (согласовать с заказчиком): Св23, Св10, Св30, Св62, Св73 — открытая лента в накладном профиле вместо «в коробе»: короба в потолке нет — высота 2650 мм < 2700 — один уровень (табл. 1.3); S2 — светорегулятор добавлен под диммируемую ленту L3; уровни сценариев выбраны конвейером; Св15 — Сдвиг под раскладку плитки стены Г на 141 мм вдоль стены — ось на шве или в центре плитки, привязка по таблице листа; Св52 — свет у зеркала — над зеркалом у умывальника по его оси (свет на лицо, а не над сантехникой); сдвиг под раскладку плитки стены А на 149 мм вдоль стены — ось на шве или в центре плитки, привязка по таблице листа.

См. лист открытых вопросов (лист 6, записи К-1, К-2, К-4, К-8).

Примечания

1. Продолжение ведомостей: лист 2 из 2 этого наименования; таблицы, прерванные на предыдущем листе, продолжены с заголовком «(продолжение)».
2. За отметку 0,000 принят уровень чистого пола. Высоты H — от чистого пола до оси изделия; привязки — от чистовой грани стены до оси механизма (у рамки на несколько постов — до оси рамки).
3. Розеточные и мокрые линии — через УЗО или дифавтомат с током утечки не более 30 мА (ПУЭ 7.1.79); в санузле выполнить ДСУП (ПУЭ 7.1.87–7.1.88).
4. Кабель — медный, исполнение нг(A)-LS (ГОСТ 31565-2012); скрытая прокладка только горизонтально и вертикально, фактические трассы зафиксировать исполнительной схемой до закрытия отделкой.
5. Расчёт нагрузок, токов КЗ, селективности и сечений — по проекту ЭОМ организации с допуском СРО; лист задаёт состав, расположение и группы.

Изм.	Кол.уч	Лист	№ док.	Подп.	Дата
Разраб.		Кырлан А.С.			04.11.26
Пров.					
ГИП					
Н. контр.					
Утв.					

ГД-2026-009-АИ

Квартира 103 м²

Общая площадь 100,72* м² · * размеры со скана, не замерены (реестр — л. 6, 7, К-1)

Дизайн-проект интерьера

Стадия	Лист	Листов
РП	27	120


Ведомость электроточек и изделий (продолжение)

М б/м

Кырлан Александр Сергеевич

Однолинейная схема щита

Щит квартирный ЩК · без масштаба

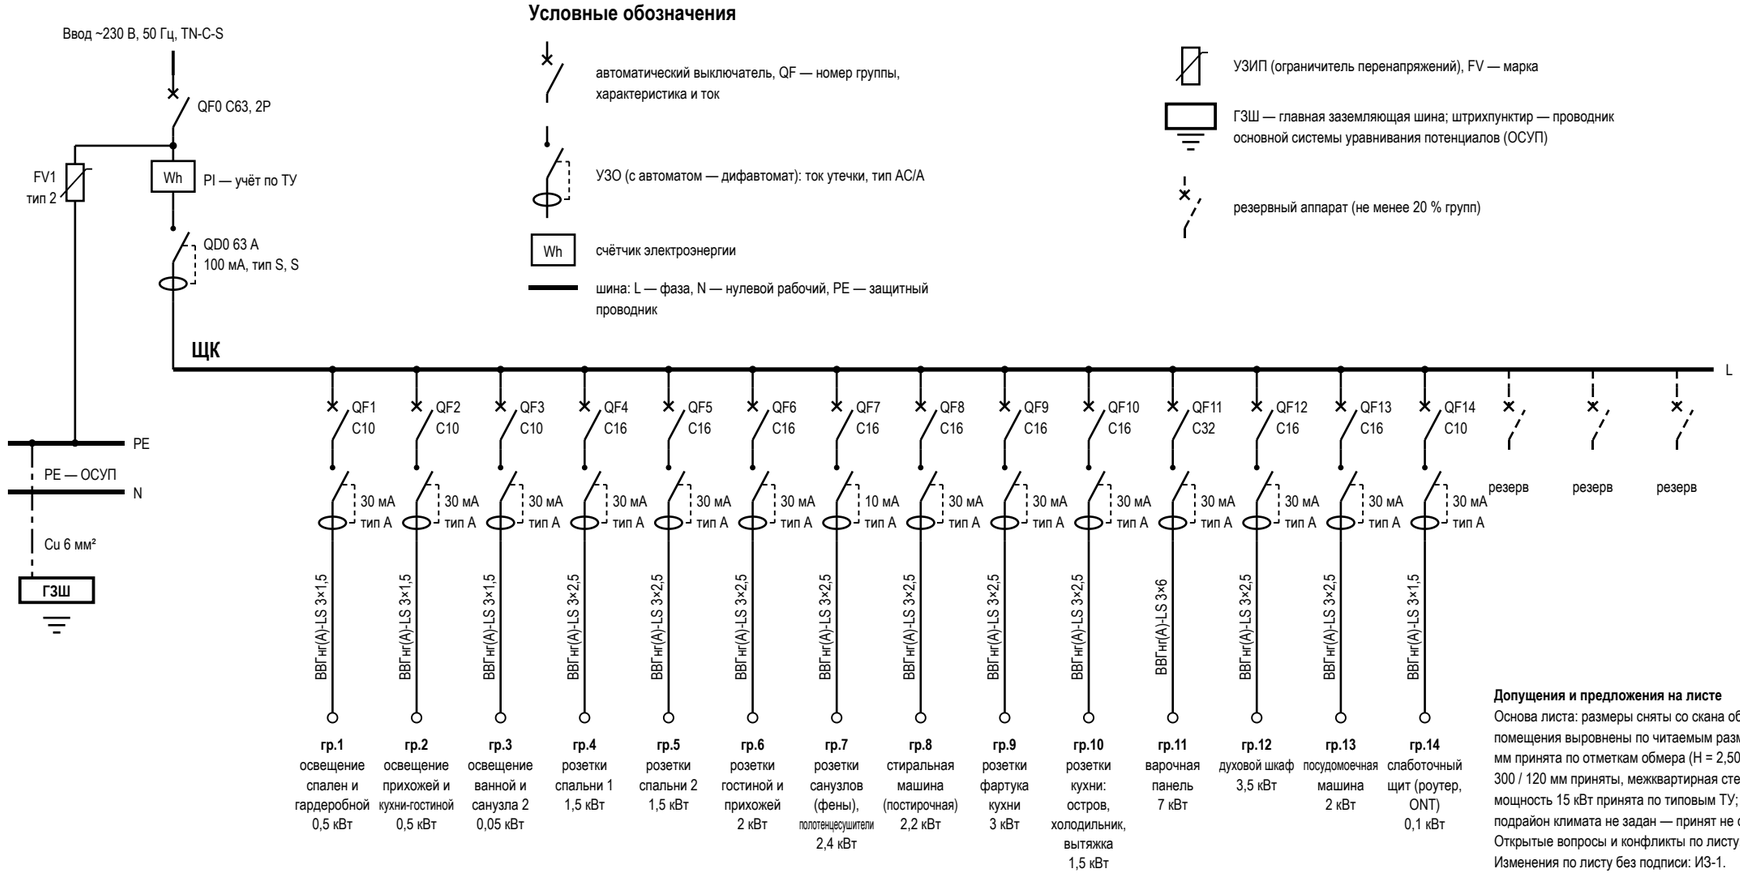

Условные обозначения

- автоматический выключатель, QF — номер группы, характеристика и ток
- УЗО (с автоматом — дифавтомат): ток утечки, тип AC/A
- Wh — счётчик электроэнергии
- шина: L — фаза, N — нулевой рабочий, PE — защитный проводник
- УЗИП (ограничитель перенапряжений), FV — марка
- ГЗШ — главная заземляющая шина; штрихпунктир — проводник основной системы уравнивания потенциалов (ОСУП)
- резервный аппарат (не менее 20 % групп)

Данные щитка

Показатель	Значение
Номер щитка	ЩК
Тип	ЩРВ-П-24, IP41
Уст. мощность, кВт	27,75
Разреш. мощность, кВт	15
Расчётная, кВт	9,8
Автоматы 1п: занят. / рез.	14 / 3
Модулей: всего / занято	24 / 20
Ток на вводе, А	63
Вводной аппарат	QF0 C63, 2P
УЗИП	FV1, тип 2, ЩК, после счётчика
ГЗШ, проводник ОСУП	Cu 6 мм²

Допущения и предложения на листе

Основа листа: размеры сняты со скана обмерного плана KV design (см): часть подписей не читается, помещения выровнены по читаемым размерам; контрольный обмер не выполнен (К-1); высота потолка 2650 мм принята по отметкам обмера (H = 2,50…2,66 м, ригель 2,28 м) — уточнить при обмере (К-2); толщины стен 300 / 120 мм приняты, межквартирная стена и колонны — по скану, не замерены (К-1); разрешённая мощность 15 кВт принята по типовым ТУ; при объединении двух квартир — переоформление ТУ (К-4); подрайон климата не задан — принят не северный (жилые от 2,5 м) (К-8).
Открытые вопросы и конфликты по листу: К-4.
Изменения по листу без подписи: ИЗ-1.
См. лист открытых вопросов (лист 6, записи ИЗ-1, К-1, К-2, К-4, К-8).

Таблица групп щита ЩК и кабельный журнал

№	Назначение	Помещения	Автомат	УЗО / дифавтомат	Кабель	Длина, м	Р, кВт	Точек
1	освещение спален и гардеробной	1, 2, 3, 5, 7, 8, 10	C10	30 мА, тип A	ВВГнг(A)-LS 3×1,5	173,6	0,5	63
2	освещение прихожей и кухни-гостиной	4, 9	C10	30 мА, тип A	ВВГнг(A)-LS 3×1,5	41	0,5	11
3	освещение ванной и санузла 2	4, 6, 10, 11	C10	30 мА, тип A	ВВГнг(A)-LS 3×1,5	53,3	0,05	11
4	розетки спальни 1	10	C16	30 мА, тип A	ВВГнг(A)-LS 3×2,5	33	1,5	4
5	розетки спальни 2	1, 3, 8	C16	30 мА, тип A	ВВГнг(A)-LS 3×2,5	75,2	1,5	15
6	розетки гостиной и прихожей	4, 9	C16	30 мА, тип A	ВВГнг(A)-LS 3×2,5	26,2	2	3
7	розетки санузлов (фены), полотенцесушители	6, 11	C16	10 мА, тип A	ВВГнг(A)-LS 3×2,5	30	2,4	4
8	стиральная машина (постирочная)	7	C16	30 мА, тип A	ВВГнг(A)-LS 3×2,5	20	2,2	1
9	розетки фартука кухни	5	C16	30 мА, тип A	ВВГнг(A)-LS 3×2,5	16,6	3	2
10	розетки кухни: остров, холодильник, вытяжка	5	C16	30 мА, тип A	ВВГнг(A)-LS 3×2,5	19	1,5	4
11	варочная панель	5	C32	30 мА, тип A	ВВГнг(A)-LS 3×6	15,8	7	1
12	духовой шкаф	5	C16	30 мА, тип A	ВВГнг(A)-LS 3×2,5	35,3	3,5	1
13	посудомоечная машина	5	C16	30 мА, тип A	ВВГнг(A)-LS 3×2,5	53	2	1
14	слаботочный щит (роутер, ONT)	4	C10	30 мА, тип A	ВВГнг(A)-LS 3×1,5	3,5	0,1	1
	Итого по сечениям ВВГнг(A)-LS, м: 3×1,5 — 271,4; 3×2,5 — 308,3; 3×6 — 15,8					595,5		

Примечания

1. Схема однолинейная: одна линия — фаза, N и PE группы; аппараты — в отключённом положении (ГОСТ 2.702, ГОСТ 2.755). Номера групп — как у точек на планах (гр.). За отметку 0,000 принят уровень чистого пола; высота щита — по плану розеток.
2. Розеточные и мокрые линии — через УЗО или дифавтомат с током утечки не более 30 мА (ПУЭ 7.1.79); в санузле выполнить ДСУП (ПУЭ 7.1.87–7.1.88).
3. УЗО тип A — для линий с электроникой, стиральной и посудомоечной машиной, LED-драйверами; тип AC — только для чисто активной нагрузки.
4. Кабель — медный, исполнение нг(A)-LS (ГОСТ 31565-2012); скрытая прокладка только горизонтально и вертикально, фактические трассы зафиксировать исполнительной схемой до закрытия отделкой.
5. Номинал автомата — не выше допустимого тока кабеля: 1,5 мм² — до 10 А, 2,5 мм² — до 16 А. Резерв щита — не менее 20 % модулей.
6. Расчёт нагрузок, токов КЗ, селективности и сечений — по проекту ЭОМ организации с допуском СРО; лист задаёт состав, расположение и группы.
7. УЗИП FV1 — после вводного автомата, проводник к шине PE — кратчайший, без петель. Шина PE щита соединяется с ГЗШ проводником ОСУП; к ГЗШ присоединяются трубы водопровода и отопления на вводе в квартиру (ПУЭ 7.1.87). Шины N и PE — раздельные, после разделения PEN не объединяются.
8. До подключения нагрузки — приёмо-сдаточные испытания с протоколом: сопротивление изоляции линий не менее 0,5 МОм, срабатывание УЗО по току и времени, непрерывность защитных проводников PE (ПУЭ, гл. 1.8).

Изм.	Кол.уч	Лист	№ док.	Подп.	Дата
Разраб.		Кырлан А.С.			04.11.26
Пров.					
ГИП					
Н. контр.					
Утв.					

ГД-2026-009-АИ

Квартира 103 м²

Общая площадь 100,72* м² · * размеры со скана, не замерены (реестр — л. 6, 7, К-1)

Дизайн-проект интерьера

Стадия	Лист	Листов
РП	28	120

Однолинейная схема щита


М б/м

Кырлан Александр Сергеевич

выпуск 04.11.2026 № 20cec94f32 · стр. 31 из 130

План принципиальных трасс

Силовые трассы и объёмы электромонтажа, слаботочка в объёмах · размеры в мм

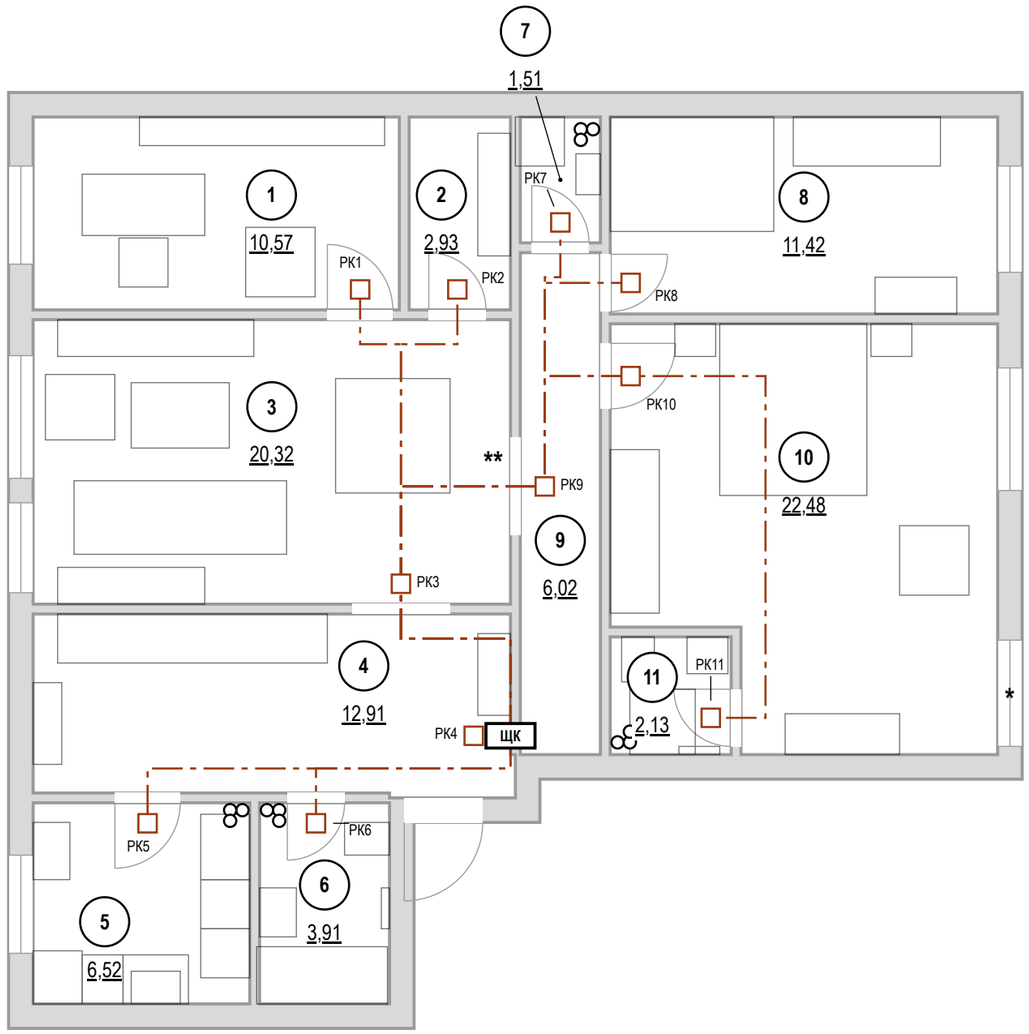

Кабель по группам ВВГнг(А)-LS, м

Гр.	мм²	Трасса	Данные
1	3×1,5	175,3	173,6
2	3×1,5	40,9	41
3	3×1,5	55,1	53,3
4	3×2,5	33	33
5	3×2,5	75,2	75,2
6	3×2,5	26,2	26,2
7	3×2,5	40,6	30

Гр.	мм²	Трасса	Данные
8	3×2,5	17,9	20
9	3×2,5	16,6	16,6
10	3×2,5	19	19
11	3×6	15,8	15,8
12	3×2,5	15,4	35,3
13	3×2,5	13,4	53
14	3×1,5	3,5	3,5
Σ		**547,9**	**595,5**

Объёмы прокладки

Работа, материал	Ед.	Кол.
Гофротруба Ø20 в потолочном пространстве	м	251,6
Кабель-канал плинтуса для силовых линий	м	129,5
Короб или накладной канал для вертикальных спусков и подъёмов	м	83,8
Коробка распределительная (РК) над дверью помещения	шт	11
Слаботочка: кабель домофона	м	4,3
Слаботочка: Кабель коаксиальный RG-6 (75 Ом) к розеткам ТВ	м	16,1
Слаботочка: U/UTP кат. 6 (LAN, Wi-Fi, камеры)	м	70,3
Слаботочка: гофротруба Ø20 отдельно от силовых	м	81,6

Экспликация помещений

№	Помещение	Площадь, м²
1	Кабинет-библиотека	10,57
2	Кладовая	2,93
3	Гостиная-столовая	20,32
4	Прихожая-холл	12,91
5	Кухня	6,52
6	Ванная	3,91
7	Постирочная	1,51
8	Спальня 2	11,42
9	Коридор	6,02
10	Спальня мастер	22,48
11	Ванная мастер	2,13
	Итого (общая площадь)	100,72

Штробы — только после заключения

Работа	Ед.	Кол.
Вертикальные штробы 20×20 мм от потолка до каждой настенной точки (в маршрут без штроб не входят)	м	103,59

Условные обозначения

- ЩК — щит квартирный
- РК — распределительная коробка над дверью помещения
- магистраль от щита к РК: потолочное пространство, гофра
- мебель и сантехприборы — подложка

Допущения и предложения на листе. Основа листа: размеры сняты со скана обмерного плана KV design (см): часть подписей не читается, помещения выровнены по читаемым размерам; контрольный обмер не выполнен (К-1); высота потолка 2650 мм принята по отметкам обмера (Н = 2,50…2,66 м, ригель 2,28 м) — уточнить при обмере (К-2); толщины стен 300 / 120 мм приняты, межквартирная стена и колонны — по скану, не замерены (К-1); разрешённая мощность 15 кВт принята по типовым ТУ; при объединении двух квартир — переоформление ТУ (К-4); подрайон климата не задан — принят не северный (жилые от 2,5 м) (К-8). Знак «*» — принято, не замерено и не подтверждено (замерить на объекте): К-6: Ст К1-3, Ст В1-3, Ст Т3-3 — положение снято со скана обмера, отдельно не замерялось; ось внутри габарита поддона См1 — обмер угла по К-6. Знак «**» — предложение проектировщика, заказчиком не утверждено (согласовать с заказчиком): ЩС — щит слаботочный: место и состав. См. лист открытых вопросов (лист 6, записи К-1, К-2, К-4–К-6, К-8).

Примечания

1. За отметку 0,000 принят уровень чистого пола. Высоты Н — от чистого пола до оси изделия; привязки — от чистовой грани стены до оси механизма (у рамки на несколько постов — до оси рамки).
2. Розеточные и мокрые линии — через УЗО или дифавтомат с током утечки не более 30 мА (ПУЭ 7.1.79); в санузле выполнить ДСУП (ПУЭ 7.1.87–7.1.88).
3. Кабель — медный, исполнение нг(А)-LS (ГОСТ 31565-2012); скрытая прокладка только горизонтально и вертикально, фактические трассы зафиксировать исполнительной схемой до закрытия отделкой.
4. Расчёт нагрузок, токов КЗ, селективности и сечений — по проекту ЭОМ организации с допуском СРО; лист задаёт состав, расположение и группы.
5. Длины — по плану: от щита вверх в потолочное пространство, по дверям и коридору без захода в мокрые помещения к распределительной коробке над дверью, далее к точкам; вертикали считаются вниз и обратно (у последней точки цепочки — в один конец); запас 10 %. Трассы принципиальные: фактическую зафиксировать исполнительной схемой до закрытия отделкой.
6. Несущие стены не определены: штробы в стенах не выполнять. Маршрут проложен без штроб: горизонтали — за потолком в гофре (251,6 м) и в кабель-канале плинтуса (129,5 м), вертикали — в коробе или накладном канале (147,4 м кабеля). Точек: за потолком — 59, спуск из потолка — 13, по плинтусу — 19, плинтус и подъём 31.
7. Вариант со штробами — работа после технического заключения: 103,59 м вертикальных штроб от потолка до каждой настенной точки; условие — только после технического заключения: стена не несущая (или вертикальная штроба в несущей согласована конструктором), глубина и ширина 20–25 мм, не в зонах 0–2 ванной. Без заключения и согласования конструктора в смету и в график эта работа не входит.
8. В данных проекта (журнал щита) длины кабеля внесены оценкой (596 м), по трассам из геометрии — 548 м (-8 %): к закупке и в смету принимать длины по трассам, а оценку в данных проекта заменить.
9. Слаботочные сети: кабели и точки считаются по лучам от ЩС** (лист слаботочных сетей): 91 м, портов патч-панели и коммутатора не менее 5; из точек 2 предложения листа слаботочки, не подтверждённые заказчиком. Изделия — в ведомости изделий.

1000 мм · печать 1:1

Изм.	Кол.уч	Лист	№ док.	Подп.	Дата
Разраб.		Кырлан А.С.			04.11.26
Пров.					
ГИП					
Н. контр.					
Утв.					

ГД-2026-009-АИ

Квартира 103 м²

Общая площадь 100,72* м² · * размеры со скана, не замерены (реестр — л. 6, 7, К-1)

Дизайн-проект интерьера

Стадия	Лист	Листов
РП	29	120

План принципиальных трасс

М 1:75


Кырлан Александр Сергеевич

выпуск 04.11.2026 № 20cec94f32 · стр. 32 из 130

План слаботочных сетей

Интернет, ТВ, домофон · размеры в мм · высоты от чистого пола

ПРЕДВАРИТЕЛЬНО · не для производства работ · открыто пунктов: 8 (реестр — л. 6, 7)

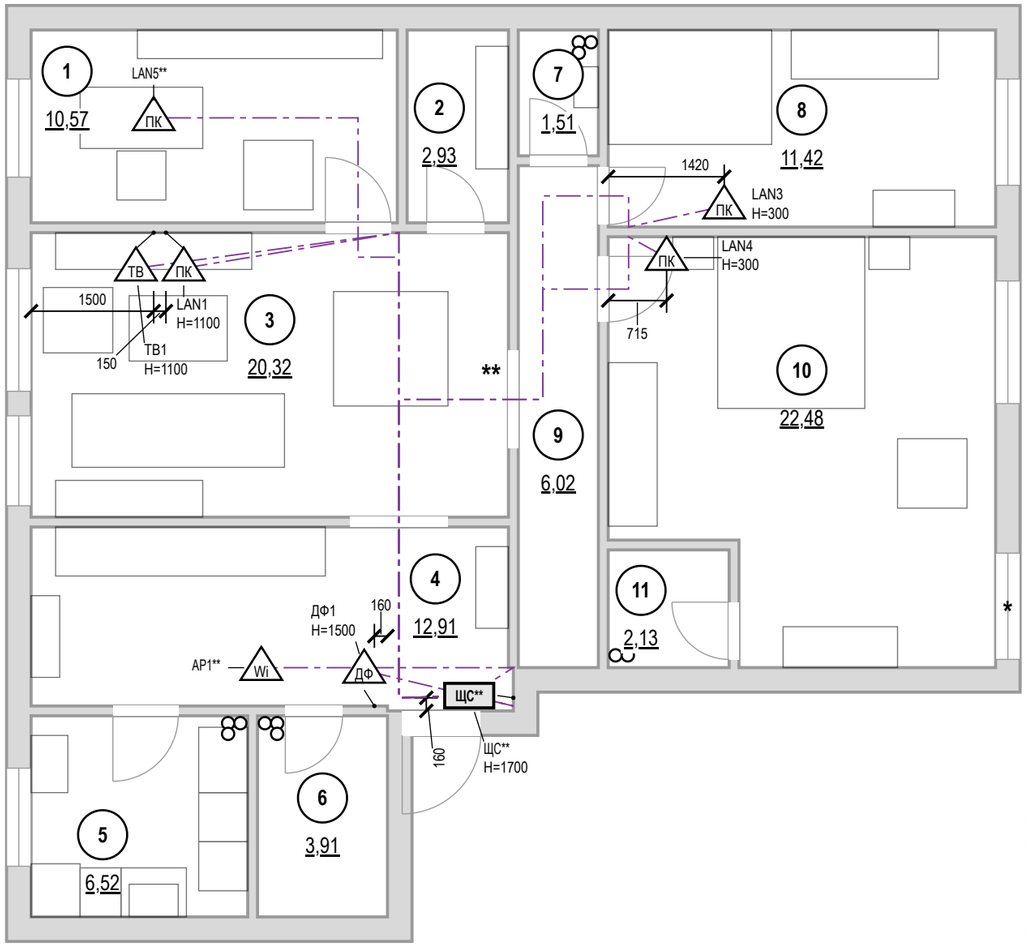

Ведомость слаботочных точек

Марка	Пом.	Назначение	H, мм	Кабель
LAN5**	1	розетка LAN (RJ45)	0	U/UTP кат. 6
ТВ1	3	розетка ТВ	1100	коаксиальный RG-6
LAN1	3	розетка LAN (RJ45)	1100	U/UTP кат. 6
ЩС**	4	щит слаботочный	1700	ввод пров.
ДФ1	4	домофон (трубка)	1500	по системе
AP1**	4	точка доступа Wi-Fi		U/UTP кат. 6
LAN3	8	розетка LAN (RJ45)	300	U/UTP кат. 6
LAN4	10	розетка LAN (RJ45)	300	U/UTP кат. 6

Условные обозначения

- **ЩС** — щит слаботочный: ввод провайдера, роутер, коммутатор
- ПК — розетка компьютерная RJ45
- ТВ — розетка телевизионная
- ДФ — трубка или монитор домофона
- Wi — точка доступа Wi-Fi (питание PoE)
- кабель от ЩС до точки, отдельным лучом
- мебель и сантехприборы — подложка
- стояк: К1 — канализация, В1 — ХВС, Т3 — ГВС
- 1 — номер помещения, площадь м²

Допущения и предложения на листе

Основа листа: размеры сняты со скана обмерного плана KV design (см): часть подписей не читается, помещения выровнены по читаемым размерам; контрольный обмер не выполнен (К-1); высота потолка 2650 мм принята по отметкам обмера (Н = 2,50…2,66 м, ригель 2,28 м) — уточнить при обмере (К-2); толщины стен 300 / 120 мм приняты, межквартирная стена и колонны — по скану, не замерены (К-1); разрешённая мощность 15 кВт принята по типовым ТУ; при объединении двух квартир — переоформление ТУ (К-4); подрайон климата не задан — принят не северный (жилые от 2,5 м) (К-8).

Знак «*» — принято, не замерено и не подтверждено (замерить на объекте): К-1: окно пом. 10 (стена Б) — Окно 1300 при offset 3500 на стене Б основной части (длина 3830) выходило за стену на 970 мм; К-6: Ст К1-3, Ст В1-3, Ст Т3-3 — положение снято со скана обмера, отдельно не замерялось; ось внутри габарита поддона См1 — обмер угла по К-6.

Знак «**» — предложение проектировщика, заказчиком не утверждено (согласовать с заказчиком): LAN5 — стол Б2 стоит посреди помещения — питание из лючка в полу под столом: трасса в конструкции пола (толщина стяжки — по обмеру) — согласовать с заказчиком; ЩС — щит слаботочный: место и состав; AP1 — точка доступа Wi-Fi: число и места; К-5: дверь пом. 3 (стена Б) — проём в межквартирной стене — объединение квартир, предложение до техзаключения.

См. лист открытых вопросов (лист 6, записи К-1, К-2, К-4–К-6, К-8).

Примечания

1. За отметку 0,000 принят уровень чистого пола. Высоты Н — от чистого пола до оси изделия; привязки — от чистовой грани стены до оси механизма (у рамки на несколько постов — до оси рамки).
2. Высота установки, не указанная на плане: розетки LAN и ТВ — 300 мм от чистого пола.
3. Слаботочные кабели — отдельно от силовых: в своей трубе или лотке, при параллельной прокладке не ближе 100 мм к силовым, пересечения под прямым углом; каждую точку — отдельным кабелем от ЩС** без скруток.
4. Трассы на листе — принципиальные; фактические зафиксировать исполнительной схемой до закрытия отделкой. Силовые линии, УЗО 30 мА, ДСУП, кабель нг(А)-LS — по листам розеток и щита.
5. Проект силовой части и расчёт токов КЗ — по проекту ЭОМ; слаботочная часть согласуется с провайдером и управляющей компанией (домофон, коллективное ТВ).

1000 мм · печать 1:1

						ГД-2026-009-АИ	
						Квартира 103 м²	
						Общая площадь 100,72* м² · * размеры со скана, не замерены (реестр — л. 6, 7, К-1)	
Изм.	Кол.уч	Лист	№ док.	Подп.	Дата		
Разраб.		Кырлан А.С.			04.11.26	Дизайн-проект интерьера	Стадия: РП; Лист: 30; Листов: 120
Пров.							
ГИП							
Н. контр.						**План слаботочных сетей**	**Кырлан Александр Сергеевич**
Утв.						М 1:75	

выпуск 04.11.2026 № 20cec94f32 · стр. 33 из 130

04

Отопление и вентиляция


Кырлан Александр Сергеевич

выпуск 04.11.2026 · 20cec94f32 · стр. 34 из 130

План вентиляции

Вытяжка, приток, переток · кондиционирование не предусмотрено · размеры в мм · высоты от чистого пола

ПРЕДВАРИТЕЛЬНО · не для производства работ · открыто пунктов: 8 (реестр — л. 6, 7)

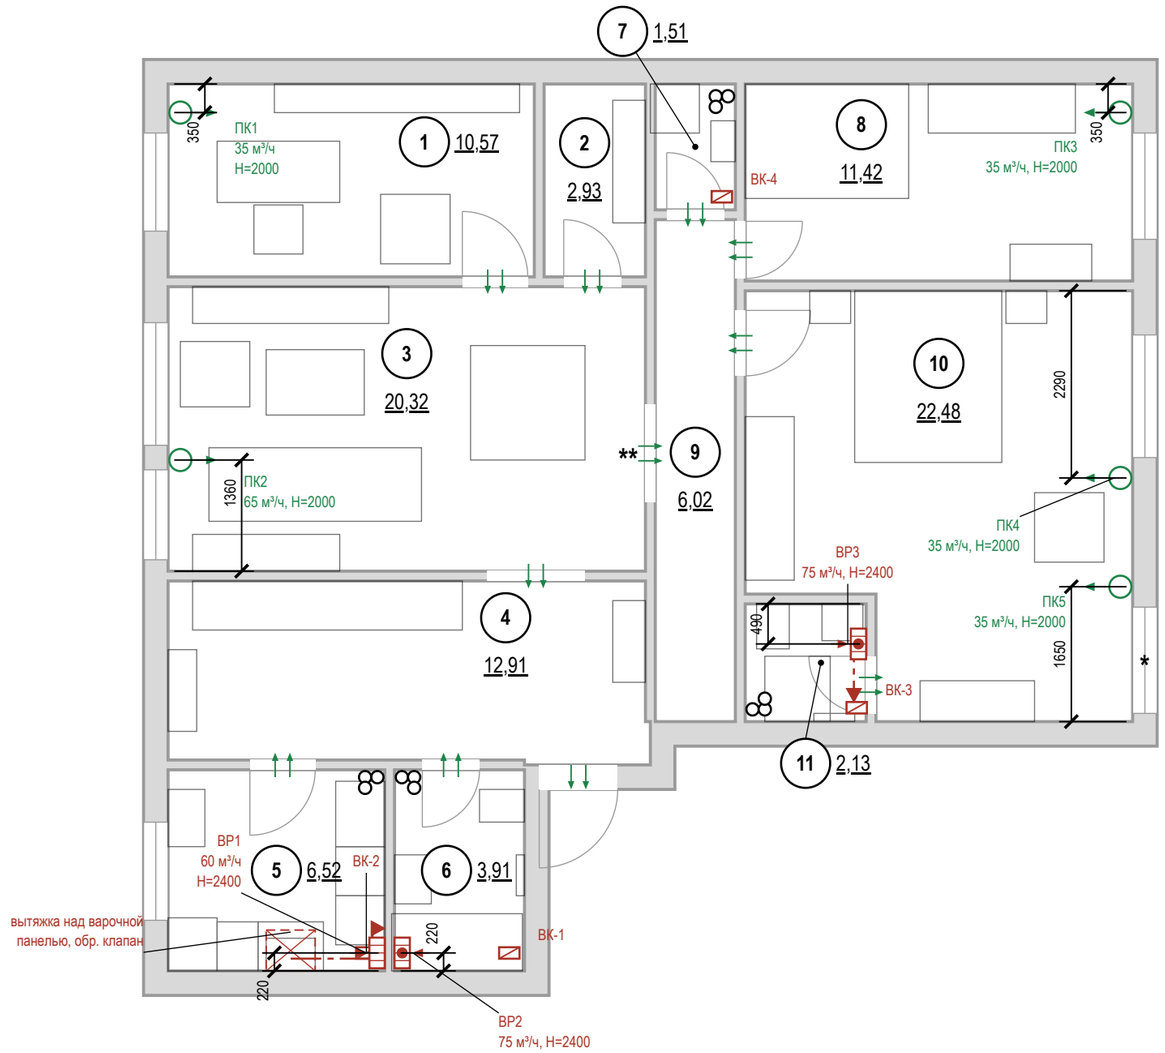

Условные обозначения

- стояк: К1 — канализация, В1 — ХВС, Т3 — ГВС
- номер помещения, площадь м²
- вытяжная решётка в вентканал: марка, расход м³/ч, H центра от чистого пола
- вытяжная решётка с бытовым вентилятором и обратным клапаном: марка, расход, H
- приточный клапан (КИВ) в наружной стене: марка, расход, H центра
- переток: зазор под полотном или переточная решётка
- кухонная вытяжка над варочной панелью
- вентканал ВК-N в стене или вентблоке
- воздуховод в коробе под потолком (за подшивным потолком) до вентканала
- отдельный вход воздуховода в вентканал, обратный клапан
- * — «*» — принято, не замерено и не подтверждено
- ** — «**» — предложение проектировщика, заказчиком не утверждено

Воздухообмен, м³/ч

№	Помещение	Выт. норма	Выт. проект	Прит. норма	Прит. проект	Устрой-ства
1	Кабинет-библиотека			32	35	ПК1
2	Кладовая	2				переток
3	Гостиная-столовая			61	65	ПК2
5	Кухня	60	60			ВР1
6	Ванная	50	75			ВР2
7	Постирочная	1				переток
8	Спальня 2			35	35	ПК3
10	Спальня мастер			68	70	ПК4, ПК5
11	Ванная мастер	50	75			ВР3
	Итого	**163**	**210**	**196**	**205**	
	Норма по жильцам: 30×2			60		

Воздухообмен квартиры — по большей из сумм притока и вытяжки: норма 196 м³/ч, проект 210 м³/ч.
Вытяжка не меньше притока — баланс сведён.

Допущения и предложения на листе

Основа листа: размеры сняты со скана обмерного плана KV design (см): часть подписей не читается, помещения выровнены по читаемым размерам; контрольный обмер не выполнен (К-1); высота потолка 2650 мм принята по отметкам обмера (H = 2,50…2,66 м, ригель 2,28 м) — уточнить при обмере (К-2); толщины стен 300 / 120 мм приняты, межквартирная стена и колонны — по скану, не замерены (К-1); разрешённая мощность 15 кВт принята по типовым ТУ; при объединении двух квартир — переоформление ТУ (К-4); подрайон климата не задан — принят не северный (жилые от 2,5 м) (К-8).
Знак «*» — принято, не замерено и не подтверждено (замерить на объекте): К-1: окно пом. 10 (стена Б) — Окно 1300 при offset 3500 на стене Б основной части (длина 3830) выходило за стену на 970 мм; К-6: Ст К1-3, Ст В1-3, Ст Т3-3 — положение снято со скана обмера, отдельно не замерялось; ось внутри габарита поддона См1 — обмер угла по К-6.
Знак «**» — предложение проектировщика, заказчиком не утверждено (согласовать с заказчиком): К-5: дверь пом. 3 (стена Б) — проём в межквартирной стене — объединение квартир, предложение до техзаключения.
См. лист открытых вопросов (лист 6, записи К-1, К-2, К-4–К-6, К-8).

Примечания

1. Расчёт систем ОВ и подбор оборудования — проектная организация с допуском СРО; лист даёт места, трассы и привязки.
2. Нормы вытяжки — СП 54.13330.2022 (Изм. 1, 2), табл. 7.1: кухня с электроплитой 60 м³/ч, с газовой 100; ванная и совмещённый санузел 50; уборная 25; гардеробная 0,2 ч⁻¹. Приток в жилые — 3 м³/ч на 1 м² (менее 20 м² общей площади на человека), иначе 30 м³/ч на человека.
3. Венткаталы и шахты не сужать, не переносить и не закрывать; вентилятор и кухонная вытяжка — через обратный клапан, без перекрытия естественной тяги; ВР3 — воздуховодом до ВК-3 ≈ 0,9 м в коробе под потолком.
4. Проектные расходы — не ниже нормы, вытяжка сведена с притоком вентиляторами мокрых помещений. Клапаны — в простенке у окна, центр 2000 мм, не над кроватью, не ближе 300 мм к стоякам отопления; типоразмер — на расход.
5. Кухонная вытяжка в воздухообмен не включена: воздуховод не менее Ø125 в коробе, вход в канал отдельный.
6. Переток — зазор под полотнами межкомнатных дверей или переточная решётка.
7. Кондиционирование заданием не предусмотрено; при установке трассы фреона и дренажа (не менее 40 мм/м, в К1 через сифон) и питание заложить до черновых работ.
8. Привязки оборудования — по паспортам приобретённых моделей, до черновых работ.
9. Знак «*» у проёма — допущение: положение проёма не замерено (окно пом. 10, стена Б); размер напечатан как принятый. Реестр: листы 6–7, вопрос К-1.
10. Клапаны ПК4, ПК5 выведены в простенок у окна, положение которого — допущение (знак «*»): после обмера окна привязку сверить.

1000 мм · печать 1:1

Изм.	Кол.уч	Лист	№ док.	Подп.	Дата
Разраб.		Кырлан А.С.			04.11.26
Пров.					
ГИП					
Н. контр.					
Утв.					

ГД-2026-009-АИ

Квартира 103 м²

Общая площадь 100,72* м² · * размеры со скана, не замерены (реестр — л. 6, 7, К-1)

Дизайн-проект интерьера

Стадия	Лист	Листов
РП	31	120

План вентиляции

М 1:75


Кырлан Александр Сергеевич

выпуск 04.11.2026 № 20cec94f32 · стр. 35 из 130

План отопления

Радиаторы, стояки, подводки · размеры в мм · высоты от чистого пола

ПРЕДВАРИТЕЛЬНО · не для производства работ · открыто пунктов: 8 (реестр — л. 6, 7)

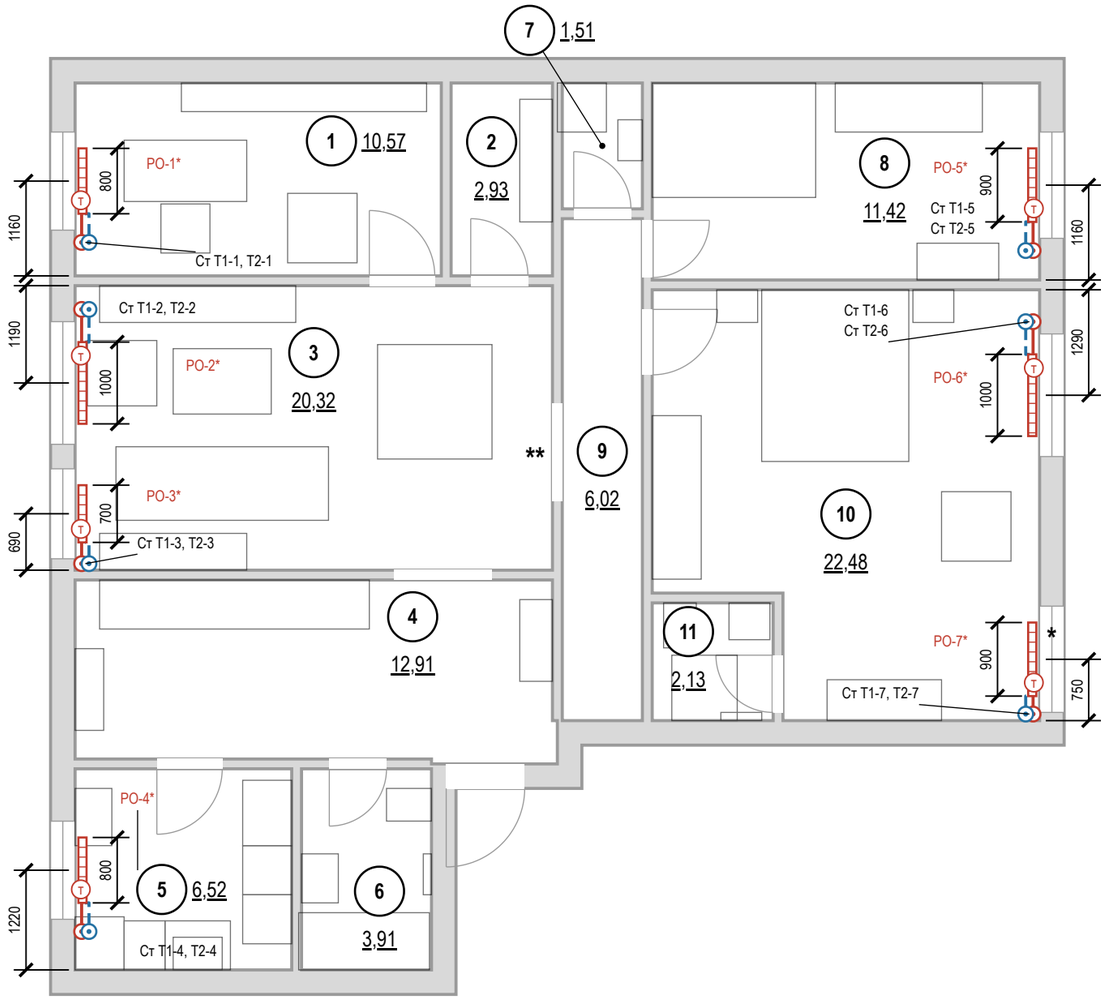

Условные обозначения

- (1) — номер помещения, площадь м²
- радиатор отопления (марка РО-N, длина по плану)
- (Т) — клапан с термоголовкой на подаче
- стояк отопления, подающий (Ст Т1-N)
- стояк отопления, обратный (Ст Т2-N)
- Т1 — отопление, подающий трубопровод
- Т2 — отопление, обратный трубопровод
- * — «*» — принято, не замерено и не подтверждено
- ** — «**» — предложение проектировщика, заказчиком не утверждено

Ведомость радиаторов

Марка	Помещение	Тип	Д×В×Г, мм	Низ / стена	Q, Вт
РО-1	1. Кабинет-библиотека	панельный*	800×400×100	120 / 40	расч.
РО-2	3. Гостиная-столовая	панельный*	1000×400×100	120 / 40	расч.
РО-3	3. Гостиная-столовая	панельный*	700×400×100	120 / 40	расч.
РО-4	5. Кухня	панельный*	800×500×100	120 / 40	расч.
РО-5	8. Спальня 2	панельный*	900×500×100	120 / 40	расч.
РО-6	10. Спальня мастер	панельный*	1000×500×100	120 / 40	расч.
РО-7	10. Спальня мастер	панельный*	900×500×100	120 / 40	расч.

* тип и мощность — по теплотехническому расчёту
Низ — от чистого пола, стена — зазор до задней панели, мм.

Привязки — до обмера
Стояки отопления в исходных данных не заданы: показаны у откосов окон, подводки — принципиально. До черновых работ — обмер стояков и паспорта приборов; лист перевыпустить по факту.

Примечания

1. Расчёт системы отопления, теплопотерь и подбор приборов — проектная организация с допуском СРО; лист даёт места и привязки.
2. Тип, длина и мощность радиаторов — по теплотехническому расчёту; лист задаёт места, зазоры и подключение.
3. Радиаторы — под каждым окном жилых комнат и кухни, центр по оси проёма, длина 0,7 ширины окна (кратно 100); окончательно — по расчёту.
4. Зазоры радиатора: низ не менее 100 мм от чистого пола, верх не менее 100 мм до подоконника, 30–50 мм от стены до задней панели; центр по оси окна с допуском ±20 мм. Верх до подоконника — 215 мм (РО-1 — 200, РО-4 — 143, РО-5 — 163, РО-6 — 205, РО-7 — 205).
5. Радиаторы не закрывать глухими коробами и мебелью; перенос и замена приборов в многоквартирном доме — переустройство, согласование с управляющей организацией (ЖК РФ ст. 25–26); вынос на лоджию запрещён.
6. Трубы отопления через межквартирные стены не прокладывать (СП 51.13330.2011, п. 9.19); через перекрытия и перегородки — в гильзах.
7. Привязки приборов и подводок — по паспортам приобретённых радиаторов и клапанов, до черновых работ.
8. До закрытия отделкой трубопроводы отопления испытать гидростатическим давлением с оформлением акта (СП 73.13330.2016, 7.2–7.3).
9. Знак «*» у проёма — допущение: положение проёма не замерено (окно пом. 10, стена Б); размер напечатан как принятый. Реестр: листы 6–7, вопрос К-1.
10. Радиатор РО-7 стоит по оси окна, положение которого — допущение (знак «*»): после обмера окна привязки прибора и подводок сверить.

Допущения и предложения на листе. Основа листа: размеры сняты со скана обмерного плана KV design (см): часть подписей не читается, помещения выровнены по читаемым размерам; контрольный обмер не выполнен (К-1); высота потолка 2650 мм принята по отметкам обмера (Н = 2,50…2,66 м, ригель 2,28 м) — уточнить при обмере (К-2); толщины стен 300 / 120 мм приняты, межквартирная стена и колонны — по скану, не замерены (К-1); разрешённая мощность 15 кВт принята по типовым ТУ; при объединении двух квартир — переоформление ТУ (К-4); подрайон климата не задан — принят не северный (жилые от 2,5 м) (К-8). Знак «*» — принято, не замерено и не подтверждено (замерить на объекте). Знак «**» — предложение проектировщика, заказчиком не утверждено (согласовать с заказчиком). См. лист открытых вопросов (лист 6, записи К-1, К-2, К-4, К-5, К-8).

1000 мм · печать 1:1

Изм.	Кол.уч	Лист	№ док.	Подп.	Дата
Разраб.		Кырлан А.С.			04.11.26
Пров.					
ГИП					
Н. контр.					
Утв.					

ГД-2026-009-АИ

Квартира 103 м²

Общая площадь 100,72* м² · * размеры со скана, не замерены (реестр — л. 6, 7, К-1)

Дизайн-проект интерьера

Стадия	Лист	Листов
РП	32	120

План отопления

М 1:75

Кырлан Александр Сергеевич

выпуск 04.11.2026 № 20cec94f32 · стр. 36 из 130

05

Водоснабжение и канализация

Кырлан Александр Сергеевич


выпуск 04.11.2026 № 20cec94f32 · стр. 37 из 130

План выводов сантехники


Выводы В1, Т3, К1 · привязки от чистовых стен · высоты от чистого пола, мм

ПРЕДВАРИТЕЛЬНО · не для производства работ · открыто пунктов: 8 (реестр — л. 6, 7)


Фрагмент 1. Ванная (пом. 6)

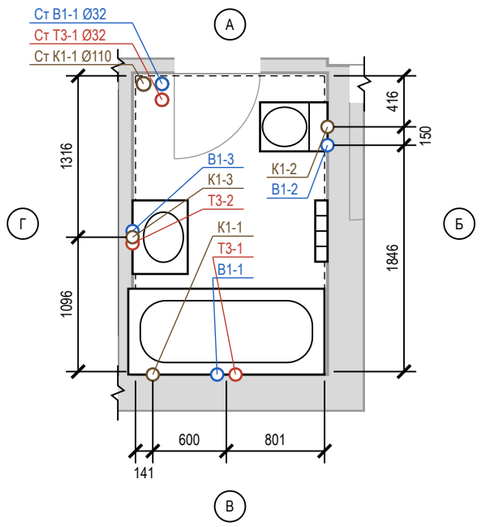


Фрагмент 2. Постирочная (пом. 7)

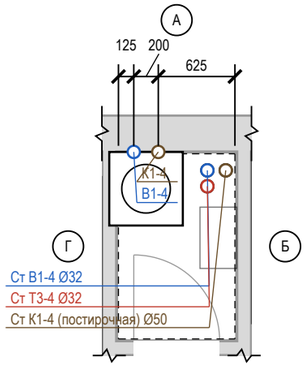

Фрагмент 3. Ванная мастер (пом. 11)

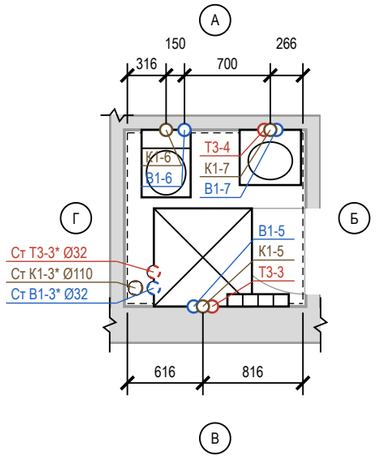

Фрагмент 4. Кухня (пом. 5)

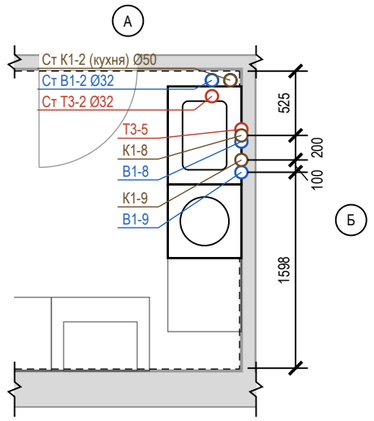

Ведомость привязок выводов

Код	Прибор	Ø	Н, мм	Привязка от чист. стен, мм	Прим.
В1-1	Сн1 ванна	½"	800*	ст. В: 666 от Г	межос. 150
Т3-1	Сн1 ванна	½"	800*	ст. В: 726 от Б	межос. 150
К1-1	Сн1 ванна	Ø50	50*	ст. В: 141 от Г	
В1-2	Сн2 унитаз подвесной	½"	250*	ст. Б: 566 от А	в раме инсталляции
К1-2	Сн2 унитаз подвесной	Ø110	220*	ст. Б: 416 от А	
В1-3	Сн3 умывальник	½"	600*	ст. Г: 1146 от В	межос. 100
Т3-2	Сн3 умывальник	½"	600*	ст. Г: 1046 от В	межос. 100
К1-3	Сн3 умывальник	Ø50	500*	ст. Г: 1096 от В	
В1-4	Пм1 стиральная машина	½"	600*	ст. А: 125 от Г	кран машины
К1-4	Пм1 стиральная машина	Ø50	600*	ст. А: 325 от Г	
В1-5	См1 душ	½"	1200*	ст. В: 541 от Г	межос. 150
Т3-3	См1 душ	½"	1200*	ст. В: 691 от Г	межос. 150
К1-5	См1 душ	Ø50	70*	ст. В: 616 от Г	сифон поддона
В1-6	См2 унитаз подвесной	½"	250*	ст. А: 466 от Г	в раме инсталляции
К1-6	См2 унитаз подвесной	Ø110	220*	ст. А: 316 от Г	
В1-7	См3 умывальник	½"	600*	ст. А: 216 от Б	межос. 100
Т3-4	См3 умывальник	½"	600*	ст. А: 316 от Б	межос. 100
К1-7	См3 умывальник	Ø50	500*	ст. А: 266 от Б	
В1-8	Кх1 мойка кухонная	½"	600*	ст. Б: 575 от А	межос. 100
Т3-5	Кх1 мойка кухонная	½"	600*	ст. Б: 475 от А	межос. 100
К1-8	Кх1 мойка кухонная	Ø50	400*	ст. Б: 525 от А	
В1-9	Кх2 посудомоечная машина	½"	550*	ст. Б: 825 от А	кран ПММ в шкафу мойки
К1-9	Кх2 посудомоечная машина	Ø40	550*	ст. Б: 725 от А	слив ПММ в шкафу мойки

* — высота по практике монтажа; сверить по паспорту прибора

Условные обозначения

- вывод В1 (код — в ведомости привязок)
- вывод Т3 (код — в ведомости привязок)
- вывод К1 (код — в ведомости привязок)
- сантехприбор по расстановке (габарит модели)
- чистовая поверхность стены (от неё привязки)
- стояк «Ст К1-N / Ст В1-N» (ГОСТ 21.601), Ø мм
- * стояк Т3 не на обмере — принят в шахте рядом со Ст В1, сверить
- * у стояка — положение принято, не замерено, сверить
- линия обрыва (граница фрагмента)
- А обозначение стены А–Г (как на развёртках)

Примечания

1. Привязки выводов даны от чистовых поверхностей стен (облицовка на сторону: ванная — 24 мм (штукатурка 10 + клей 5 + плитка 9); постирочная — 15 мм (штукатурка 10 + шпаклёвка 5 (принято)); ванная мастер — 24 мм (штукатурка 10 + клей 5 + плитка 9); кухня — 22 мм (фартук: штукатурка 10 + клей 3 + плитка 9)); эти же грани — на развёртках и в раскладке плитки. Высоты — от чистого пола помещения.
2. Высоты и межосевые, отмеченные «*», приняты по практике монтажа; до черновой разводки сверить по паспорту выбранного прибора (смеситель, инсталляция, сифон).
3. Горячая вода (Т3) — слева от холодной (В1), если смотреть на прибор. Допуск установки выводов: ±5 мм в группе, ±20 мм у отдельно стоящих.
4. Расчёт систем водоснабжения и канализации и подбор оборудования выполняет проектная организация; лист задаёт места и высоты выводов.
5. Посудомоечная машина Кх2: кран и слив — отдельными выводами в шкафу мойки (не за машиной), до машины ≤ 1500 мм.
6. Прибор Кх1 мойка кухонная, Кх2 посудомоечная машина взят из расстановки мебели (по шкафу с мойкой).
7. Ст К1-3*, Ст В1-3*, Ст Т3-3* на обмере не показаны: положение принято, не замерено (К-6); положение сверить на объекте до разметки.
8. Стояки в коробах/шахтах не замоноличивать; стояк К1 в коробе — звукоизоляция стояка в коробе без жёсткого контакта с трубой; к арматуре и ревизиям — люк не меньше 300×400.
9. Знак «*» у стояка — положение принято, не замерено (Ст К1-3*, Ст В1-3*, Ст Т3-3*); сверить на объекте до разметки. Реестр: листы 6–7, вопрос К-6.

1000 мм · печать 1:1

Допущения и предложения на листе. Знак «*» принято (замерить). См. лист открытых вопросов (лист 6).

Изм.	Кол.уч	Лист	№ док.	Подп.	Дата	ГД-2026-009-АИ			
						Квартира 103 м²			
						Общая площадь 100,72* м² · * размеры со скана, не замерены (реестр — л. 6, 7, К-1)			
Разраб.		Кырлан А.С.			04.11.26	Дизайн-проект интерьера	Стадия	Лист	Листов
Пров.							РП	33	120
ГИП						План выводов сантехники	Кырлан Александр Сергеевич		
Н. контр.						М 1:50			
Утв.									


выпуск 04.11.2026 № 20cec94f32 · стр. 38 из 130

Схема разводки водопровода и канализации


Схемы систем В1, Т3, К1 · трассы принципиальные · уклоны в мм на 1 м · план М 1:200, фрагменты М 1:40

ПРЕДВАРИТЕЛЬНО · не для производства работ · открыто пунктов: 8 (реестр — л. 6, 7)

План квартиры (М 1:200)

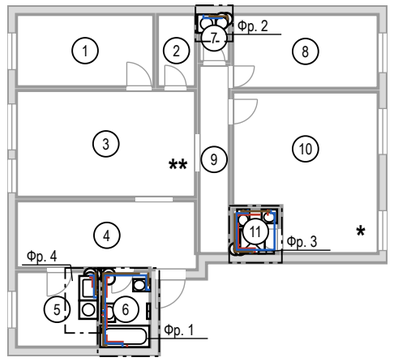

Узел ввода В1, Т3 (схема, без масштаба)

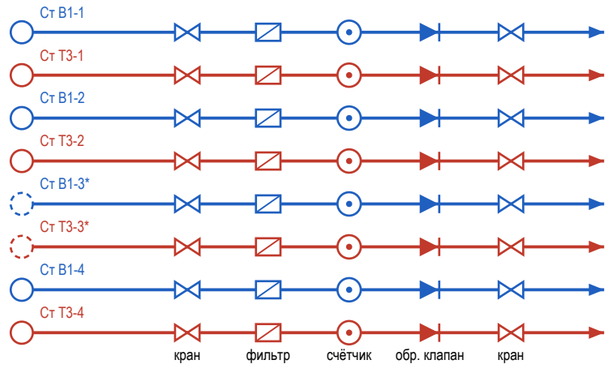


состав узла — по согласованию

⊗ Ст К1-1, Ст К1-2 (кухня), Ст К1-3*, Ст К1-4 (постирочная): ревизия на стояке — люк в коробе


Условные обозначения

- В1 — водопровод хозяйственно-питьевой (ХВС), PP-R Ø20
- Т3 — горячее водоснабжение, подача (ГВС), PP-R Ø20
- К1 — канализация бытовая
- направление уклона К1 / пола: Ø, мм на 1 м
- ⊗ ревизия (прочистка) К1 — доступ сохранить
- • тройник (ответвление к прибору)
- короб К1 над чистым полом (ГКЛВ под плитку)
- ○ вывод В1 (код — в ведомости привязок)
- ○ вывод Т3 (код — в ведомости привязок)
- ○ вывод К1 (код — в ведомости привязок)
- сантехприбор по расстановке (габарит модели)
- ○ стояк «Ст К1-N / Ст В1-N» (ГОСТ 21.601), Ø мм
- ○ * стояк Т3 не на обмере — принят в шахте рядом со Ст В1, сверить
- * у стояка — положение принято, не замерено, сверить
- линия обрыва (граница фрагмента)
- граница фрагмента на плане (Фр. N)


Фр. 1. Ванная (М 1:40)

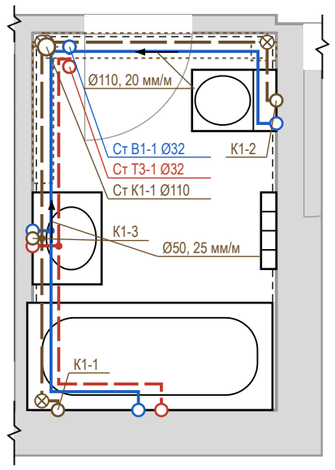


Фр. 2. Постирочная (М 1:40)

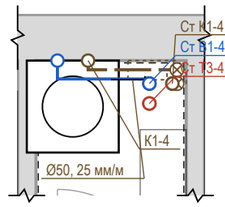

Фр. 3. Ванная мастер (М 1:40)

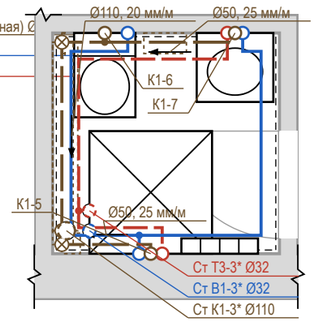

Фр. 4. Кухня (М 1:40)

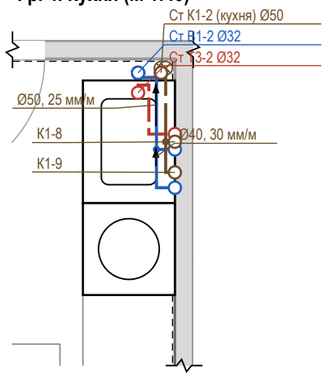

Профиль выпусков К1 (до врезки в стояк)

Выпуск	Прибор	Ø	L, м	i, мм/м	Δh, мм	Прокладка, мм
К1-2	Сн2 унитаз подвесной	Ø110	1,91	20	38	под проёмом Д-5: короба нет; К-7
К1-6	См2 унитаз подвесной	Ø110	1,60	20	32	короб 180×140
К1-1	Сн1 ванна	Ø50	2,56	25	64	короб 150×110
К1-7	См3 умывальник	Ø50	2,45	25	61	короб 150×110
К1-3	Сн3 умывальник	Ø50	1,40	25	35	короб 120×110
К1-4	Пм1 стиральная машина	Ø50	0,76	25	19	короб 100×110
К1-5	См1 душ	Ø50	0,76	25	19	короб 100×110
К1-8	Кх1 мойка кухонная	Ø50	0,60	25	15	над полом за приборами
К1-9	Кх2 посудомоечная машина	Ø40	0,80	30	24	над полом за приборами

Короб h×b: h — от чистого пола, b — от чистовой стены. Стяжка 35 мм — лист полов.

Примечания

1. Трассы принципиальные, построены от стояков вдоль стен помещений; фактическое положение фиксируется исполнительной схемой с привязками (фото с рулеткой) до закрытия.
2. Уклон К1 не менее 1/d и не более 150 мм/м (СП 30.13330.2020, п. 19.1), приняты практические уклоны; поворот — двумя отводами 45°, ревизия после поворота, доступ сохранить. Стояк К1 в коробе — звукоизоляция стояка в коробе, без жёсткого контакта короба с трубой.
3. Решение по К1: стяжка 35 мм не укрывает трубы (нужно Ø + Δh + 45 мм) — выпуски идут над чистым полом вдоль стен: К1-8, К1-9 — за приборами и в раме инсталляции; К1-6, К1-1, К1-7, К1-3, К1-4, К1-5 — в коробе ГКЛВ под плитку (размеры в профиле). Короба — на развёртках; отметку низа врезки в стояк замерить до черновых работ.
4. К1-2 (Сн2 унитаз подвесной): трасса К1 до Ст К1-1 — под проёмом Д-5, короб там не поставить: прибор ближе к стояку, выпуск в полу с подъёмом пола или насосная установка (КНС) — решение К-7; до решения не выполнять.
5. Состав узла ввода В1, Т3 — по согласованию: на схеме типовой узел — кран шаровой, фильтр, счётчик, обратный клапан, кран; состав и места не определены (записи реестра нет). Доступ к арматуре — через люк не меньше 300×400. Водопровод — в штробе стен или в коробах; трубы испытать давлением до закрытия (акт скрытых работ).
6. Расчёт систем, диаметры магистралей и подбор оборудования выполняет проектная организация; врезка и перенос стояков — по согласованию с управляющей организацией. Арматуру и привязки сверить по паспортам приборов.
7. Ст К1-3*, Ст В1-3*, Ст Т3-3* на обмере не показаны: положение принято, не замерено (К-6); положение сверить на объекте до разводки.
8. Знак «*» у стояка — положение принято, не замерено (Ст К1-3*, Ст В1-3*, Ст Т3-3*); сверить на объекте до разметки. Реестр: листы 6–7, вопрос К-6.

Допущения и предложения на листе. Знак «*» принято (замерить). Знак «**» предложено (согласовать). См. лист открытых вопросов (лист 6).

Изм.	Кол.уч	Лист	№ док.	Подп.	Дата
Разраб.		Кырлан А.С.			04.11.26
Пров.					
ГИП					
Н. контр.					
Утв.					

ГД-2026-009-АИ

Квартира 103 м²

Общая площадь 100,72* м² · * размеры со скана, не замерены (реестр — л. 6, 7, К-1)

Дизайн-проект интерьера

Стадия	Лист	Листов
РП	34	120

Схема разводки водопровода и канализации

М 1:200; 1:40


Кырлан Александр Сергеевич

выпуск 04.11.2026 № 20cec94f32 · стр. 39 из 130

Аксонометрическая схема В1 (холодное водоснабжение)

аксонометрия · диаметры, уклоны, отметки, стояки и приборы · трассы принципиальные

Схема В1 (М 1:100; по вертикали и горизонтали один масштаб, глубина — ×0,5 под 45°)

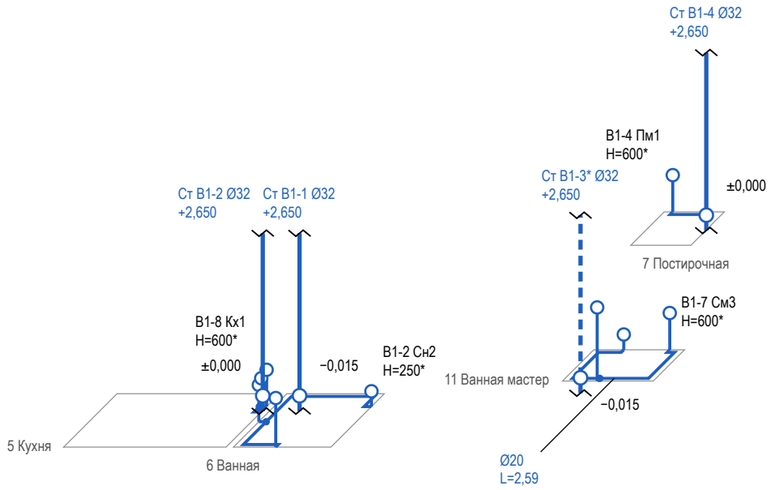

Условные обозначения

- В1 — водопровод хозяйственно-питьевой (ХВС), PP-R Ø20
- вывод В1 (код — в ведомости привязок)
- стояк «Ст К1-N / Ст В1-N» (ГОСТ 21.601), Ø мм
- стояк в плане (на отметке пола); вертикаль — стояк по высоте, разрыв — перекрытие
- тройник (ответвление к прибору)
- кран шаровой
- * стояк Т3 не на обмере — принят в шахте рядом со Ст В1, сверить

Допущения и предложения на листе

Основа листа: размеры сняты со скана обмерного плана KV design (см): часть подписей не читается, помещения выровнены по читаемым размерам; контрольный обмер не выполнен (К-1); высота потолка 2650 мм принята по отметкам обмера (Н = 2,50…2,66 м, ригель 2,28 м) — уточнить при обмере (К-2); толщины стен 300 / 120 мм приняты, межквартирная стена и колонны — по скану, не замерены (К-1); разрешённая мощность 15 кВт принята по типовым ТУ; при объединении двух квартир — переоформление ТУ (К-4); подрайон климата не задан — принят не северный (жилые от 2,5 м) (К-8).

Знак «*» — принято, не замерено и не подтверждено (замерить на объекте): К-6: Ст В1-3, Ст К1-3, Ст Т3-3 — положение снято со скана обмера, отдельно не замерялось; ось внутри габарита поддона См1 — обмер угла по К-6.

См. лист открытых вопросов (лист 6, записи К-1, К-2, К-4, К-6, К-8).

Примечания

1. Схема В1 построена по тем же трассам, что план разводки: положение в плане сохранено, глубина — в масштабе ×0,5. Трассы принципиальные; фактическое положение фиксируется исполнительной схемой до закрытия.
2. Высоты Н — от чистого пола помещения, мм. Отметка прокладки магистрали В1 (в стяжке, в стене или по полу) в данных не задана: участки показаны на уровне пола условно (записи реестра нет).
3. * — высота вывода принята по практике монтажа; сверить по паспорту прибора.
4. Узел ввода В1 (кран, фильтр, счётчик, обратный клапан, кран) — на схеме разводки; состав узла ввода — по согласованию. Кран шаровой — на первом участке от стояка.
5. Ст В1-3* на обмере не показаны: положение принято, не замерено (К-6); положение сверить на объекте до разводки.
6. Трубы испытать давлением до закрытия (акт скрытых работ, опрессовка по СП 73.13330.2016).
7. Диаметры, высоты выводов и места кранов — по паспортам выбранных приборов и расчёту проектной организации.
8. Расчёт систем, диаметры магистралей и подбор оборудования выполняет проектная организация.

1000 мм · печать 1:1

Изм.	Кол.уч	Лист	№ док.	Подп.	Дата
Разраб.		Кырлан А.С.			04.11.26
Пров.					
ГИП					
Н. контр.					
Утв.					

ГД-2026-009-АИ

Квартира 103 м²

Общая площадь 100,72* м² · * размеры со скана, не замерены (реестр — л. 6, 7, К-1)

Дизайн-проект интерьера

Стадия	Лист	Листов
РП	35	120

Аксонометрическая схема В1 (холодное водоснабжение)

М 1:100

Кырлан Александр Сергеевич


ПРЕДВАРИТЕЛЬНО · не для производства работ · открыто пунктов: 8 (реестр — л. 6, 7)

выпуск 04.11.2026 № 20cec94f32 · стр. 40 из 130

Аксонометрическая схема Т3 (горячее водоснабжение)

аксонометрия · диаметры, уклоны, отметки, стояки и приборы · трассы принципиальные

Схема Т3 (М 1:100; по вертикали и горизонтали один масштаб, глубина — ×0,5 под 45°)

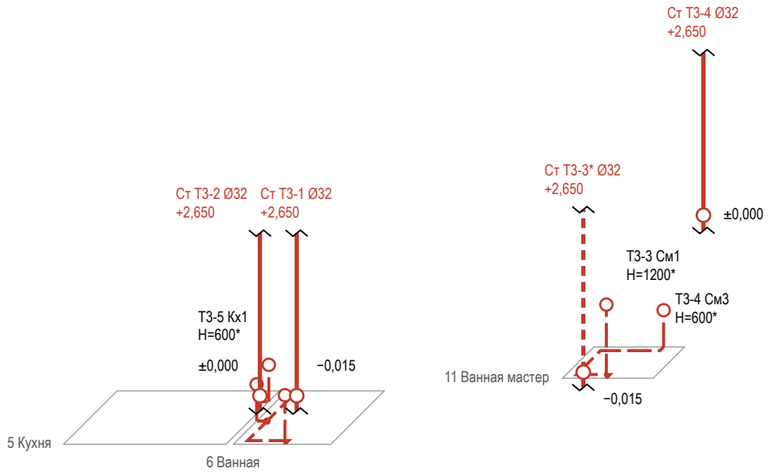

ПРЕДВАРИТЕЛЬНО · не для производства работ · открыто пунктов: 8 (реестр — л. 6, 7)

Условные обозначения

- Т3 — горячее водоснабжение, подача (ГВС), PP-R Ø20
- вывод Т3 (код — в ведомости привязок)
- стояк «Ст К1-N / Ст В1-N» (ГОСТ 21.601), Ø мм
- стояк в плане (на отметке пола); вертикаль — стояк по высоте, разрыв — перекрытие
- тройник (ответвление к прибору)
- кран шаровой
- * стояк Т3 не на обмере — принят в шахте рядом со Ст В1, сверить

Допущения и предложения на листе

Основа листа: размеры сняты со скана обмерного плана KV design (см): часть подписей не читается, помещения выровнены по читаемым размерам; контрольный обмер не выполнен (К-1); высота потолка 2650 мм принята по отметкам обмера (Н = 2,50…2,66 м, ригель 2,28 м) — уточнить при обмере (К-2); толщины стен 300 / 120 мм приняты, межквартирная стена и колонны — по скану, не замерены (К-1); разрешённая мощность 15 кВт принята по типовым ТУ; при объединении двух квартир — переоформление ТУ (К-4); подрайон климата не задан — принят не северный (жилые от 2,5 м) (К-8).

Знак «*» — принято, не замерено и не подтверждено (замерить на объекте): К-6: Ст Т3-3, Ст К1-3, Ст В1-3 — положение снято со скана обмера, отдельно не замерялось; ось внутри габарита поддона См1 — обмер угла по К-6.

См. лист открытых вопросов (лист 6, записи К-1, К-2, К-4, К-6, К-8).

Примечания

1. Схема Т3 построена по тем же трассам, что план разводки: положение в плане сохранено, глубина — в масштабе ×0,5. Трассы принципиальные; фактическое положение фиксируется исполнительной схемой до закрытия.
2. Высоты Н — от чистого пола помещения, мм. Отметка прокладки магистрали Т3 (в стяжке, в стене или по полу) в данных не задана: участки показаны на уровне пола условно (записи реестра нет).
3. * — высота вывода принята по практике монтажа; сверить по паспорту прибора.
4. Узел ввода Т3 (кран, фильтр, счётчик, обратный клапан, кран) — на схеме разводки; состав узла ввода — по согласованию. Кран шаровой — на первом участке от стояка.
5. Циркуляция ГВС в данных не задана — циркуляционного трубопровода на схеме нет (записи реестра нет).
6. Ст Т3-3* на обмере не показаны: положение принято, не замерено (К-6); положение сверить на объекте до разводки.
7. Трубы испытать давлением до закрытия (акт скрытых работ, опрессовка по СП 73.13330.2016).
8. Диаметры, высоты выводов и места кранов — по паспортам выбранных приборов и расчёту проектной организации.
9. Расчёт систем, диаметры магистралей и подбор оборудования выполняет проектная организация.

1000 мм · печать 1:1

Изм.	Кол.уч	Лист	№ док.	Подп.	Дата
Разраб.		Кырлан А.С.			04.11.26
Пров.					
ГИП					
Н. контр.					
Утв.					

ГД-2026-009-АИ

Квартира 103 м²

Общая площадь 100,72* м² · * размеры со скана, не замерены (реестр — л. 6, 7, К-1)

Дизайн-проект интерьера	Стадия	Лист	Листов
	РП	36	120

Аксонометрическая схема Т3 (горячее водоснабжение)

М 1:100


Кырлан Александр Сергеевич

выпуск 04.11.2026 № 20cec94f32 · стр. 41 из 130

Аксонометрическая схема К1 (канализация)

аксонометрия · диаметры, уклоны, отметки, стояки и приборы · трассы принципиальные

Схема К1 (М 1:100; по вертикали и горизонтали один масштаб, глубина — ×0,5 под 45°)

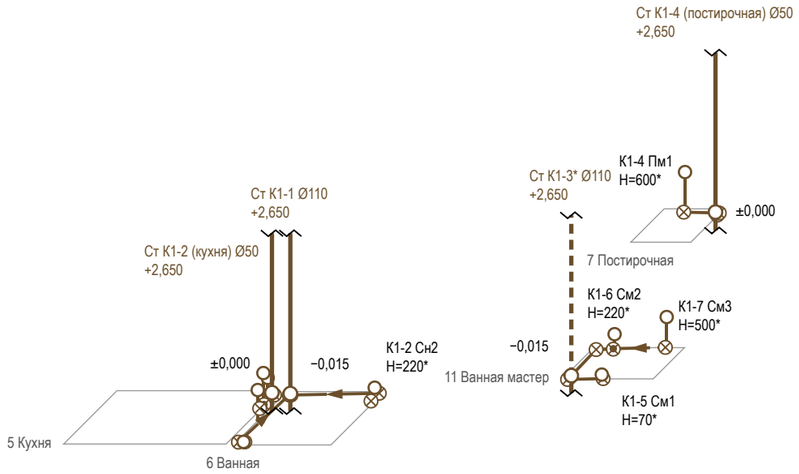

ПРЕДВАРИТЕЛЬНО · не для производства работ · открыто пунктов: 8 (реестр — л. 6, 7)

Условные обозначения

- К1 — канализация бытовая
- вывод К1 (код — в ведомости привязок)
- стояк «Ст К1-N / Ст В1-N» (ГОСТ 21.601), Ø мм
- стояк в плане (на отметке пола); вертикаль — стояк по высоте, разрыв — перекрытие
- направление уклона К1 / пола: Ø, мм на 1 м
- ревизия (прочистка) К1 — доступ сохранить
- тройник (ответвление к прибору)
- * стояк Т3 не на обмере — принят в шахте рядом со Ст В1, сверить

Допущения и предложения на листе

Основа листа: размеры сняты со скана обмерного плана KV design (см): часть подписей не читается, помещения выровнены по читаемым размерам; контрольный обмер не выполнен (К-1); высота потолка 2650 мм принята по отметкам обмера (Н = 2,50…2,66 м, ригель 2,28 м) — уточнить при обмере (К-2); толщины стен 300 / 120 мм приняты, межквартирная стена и колонны — по скану, не замерены (К-1); разрешённая мощность 15 кВт принята по типовым ТУ; при объединении двух квартир — переоформление ТУ (К-4); подрайон климата не задан — принят не северный (жилые от 2,5 м) (К-8).

Знак «*» — принято, не замерено и не подтверждено (замерить на объекте): К-6: Ст К1-3, Ст В1-3, Ст Т3-3 — положение снято со скана обмера, отдельно не замерялось; ось внутри габарита поддона См1 — обмер угла по К-6.

См. лист открытых вопросов (лист 6, записи К-1, К-2, К-4, К-6, К-8).

Примечания

1. Схема К1 построена по тем же трассам, что план разводки: положение в плане сохранено, глубина — в масштабе ×0,5. Трассы принципиальные; фактическое положение фиксируется исполнительной схемой до закрытия.
2. Отметки — от плиты перекрытия: низ трубы у врезки в стояк — отметка из данных выпуска, к прибору труба поднимается на уклон i, мм/м (уклон не менее 1/d и не более 150 мм/м, СП 30.13330.2020, п. 19.1); чистый пол — выше плиты на стяжку (высота пирога пола). Высота выпуска прибора Н — от чистого пола.
3. * — высота вывода принята по практике монтажа; сверить по паспорту прибора.
4. Ревизия — на повороте и в начале участка; стояк К1 в коробе с люком — звукоизоляция стояка в коробе; поворот — двумя отводами 45°.
5. Ст К1-3* на обмере не показаны: положение принято, не замерено (К-6); положение сверить на объекте до разводки.
6. Трубы испытать давлением до закрытия (акт скрытых работ, опрессовка по СП 73.13330.2016).
7. Диаметры, высоты выводов и места кранов — по паспортам выбранных приборов и расчёту проектной организации.
8. Расчёт систем, диаметры магистралей и подбор оборудования выполняет проектная организация.

1000 мм · печать 1:1

Изм.	Кол.уч	Лист	№ док.	Подп.	Дата
Разраб.		Кырлан А.С.			04.11.26
Пров.					
ГИП					
Н. контр.					
Утв.					

ГД-2026-009-АИ

Квартира 103 м²

Общая площадь 100,72* м² · * размеры со скана, не замерены (реестр — л. 6, 7, К-1)

Дизайн-проект интерьера

Стадия	Лист	Листов
РП	37	120

Аксонометрическая схема К1 (канализация)

М 1:100


Кырлан Александр Сергеевич

выпуск 04.11.2026 № 20cec94f32 · стр. 42 из 130

Развёртки мокрых зон: выводы ВК. Кухня

пом. 5 · выводы В1, Т3, К1 на стенах · высоты от чистого пола, привязки от чистовых углов, мм

Стена Б (М 1:20)

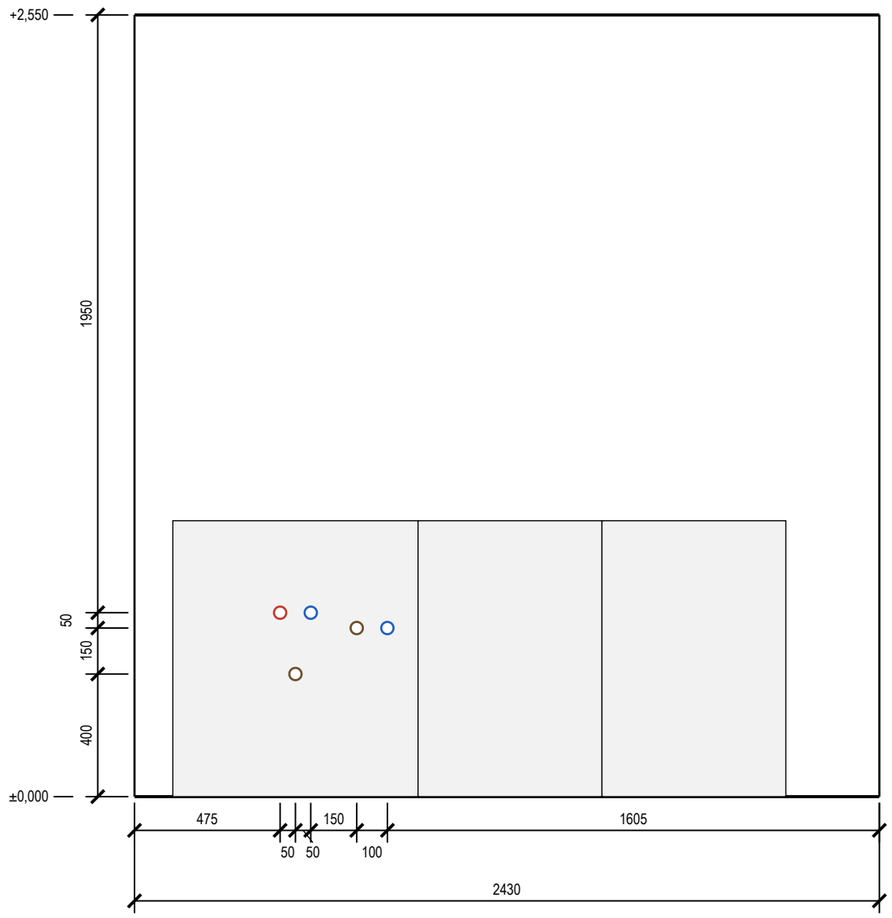

Допущения и предложения на листе

Основа листа: размеры сняты со скана обмерного плана KV design (см): часть подписей не читается, помещения выровнены по читаемым размерам; контрольный обмер не выполнен (К-1); высота потолка 2650 мм принята по отметкам обмера (Н = 2,50…2,66 м, ригель 2,28 м) — уточнить при обмере (К-2); толщины стен 300 / 120 мм приняты, межквартирная стена и колонны — по скану, не замерены (К-1); разрешённая мощность 15 кВт принята по типовым ТУ; при объединении двух квартир — переоформление ТУ (К-4); подрайон климата не задан — принят не северный (жилые от 2,5 м) (К-8).

См. лист открытых вопросов (лист 6, записи К-1, К-2, К-4, К-8).

Ведомость привязок выводов (от чистого пола и угла)

Код	Прибор	Ø	Н, мм	Привязка, мм
В1-8	Кх1 мойка кухонная	½"	600*	ст. Б: 575 от лев. угла
Т3-5	Кх1 мойка кухонная	½"	600*	ст. Б: 475 от лев. угла
К1-8	Кх1 мойка кухонная	Ø50	400*	ст. Б: 525 от лев. угла

Ведомость привязок (продолжение)

Код	Прибор	Ø	Н, мм	Привязка, мм
В1-9	Кх2 посудомоечная машина	½"	550*	ст. Б: 825 от лев. угла
К1-9	Кх2 посудомоечная машина	Ø40	550*	ст. Б: 725 от лев. угла

Условные обозначения

- вывод В1 (код — в ведомости привязок)
- вывод Т3 (код — в ведомости привязок)
- вывод К1 (код — в ведомости привязок)
- сантехприбор по расстановке (габарит модели)
- дверной проём; окно — сплошной контур

Примечания

1. Габариты и высоты приборов, межосевые смесителей и места кранов — по паспортам выбранных приборов, сверяются до разметки стен.
2. Высоты Н — от чистого пола помещения, мм; отметка чистого пола и потолка — у левого края вида (от ±0,000 объекта). Привязки — от левого чистового угла вида (облицовка стен вычтена), как на развёртках стен.
3. * — высота принята по практике монтажа: в данных прибора её нет; до разметки стен сверить по паспорту выбранного прибора (смеситель, инсталляция, сифон).
4. Стояки в помещении: Ст К1-2 (кухня) Ø50, Ст В1-2 Ø32, Ст Т3-2 Ø32 — положение на плане выводов; выводы подключаются к ним по схеме разводки.
5. Ревизионные люки к арматуре и ревизиям в данных не заданы: место и размер не определены (записи реестра нет).
6. Мойка, ПММ и фильтр — выводы в шкафу мойки; диаметры и положение сифона и кранов сверить по паспортам приборов и чертежам модуля.
7. Часть подписей выводов не уместилась у знака: коды и высоты — в ведомости привязок.
8. Расчёт систем водоснабжения и канализации и подбор оборудования выполняет проектная организация; лист задаёт места и высоты выводов.

1000 мм · печать 1:1

Изм.	Кол.уч	Лист	№ док.	Подп.	Дата
Разраб.		Кырлан А.С.			04.11.26
Пров.					
ГИП					
Н. контр.					
Утв.					

ГД-2026-009-АИ

Квартира 103 м²

Общая площадь 100,72* м² · * размеры со скана, не замерены (реестр — л. 6, 7, К-1)

Дизайн-проект интерьера

Стадия	Лист	Листов
РП	38	120

Развёртки мокрых зон: выводы ВК. Кухня

М 1:20

Кырлан Александр Сергеевич


выпуск 04.11.2026 № 20cec94f32 · стр. 43 из 130

Развёртки мокрых зон: выводы ВК. Ванная


пом. 6 · выводы В1, Т3, К1 на стенах · высоты от чистого пола, привязки от чистовых углов, мм

ПРЕДВАРИТЕЛЬНО · не для производства работ · открыто пунктов: 8 (реестр — л. 6, 7)


Стена Б (М 1:25)

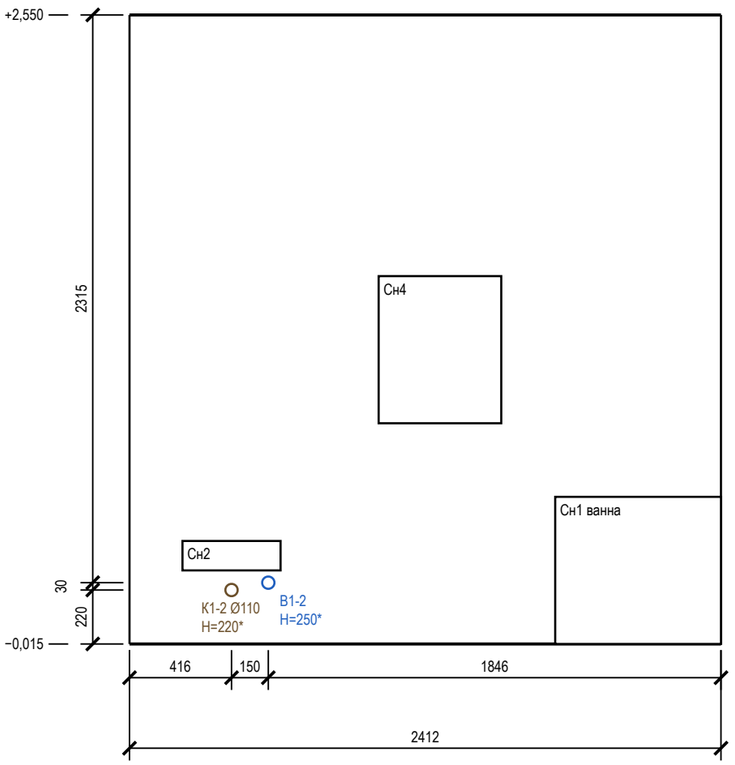

Стена В (М 1:25)

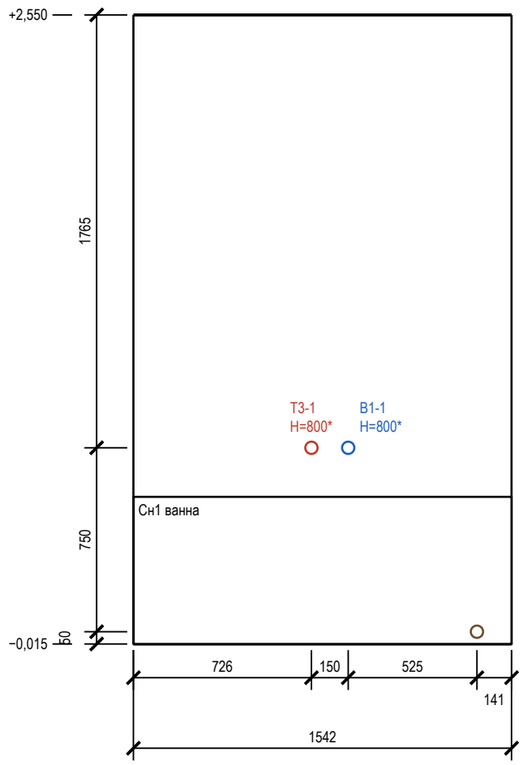

Стена Г (М 1:25)

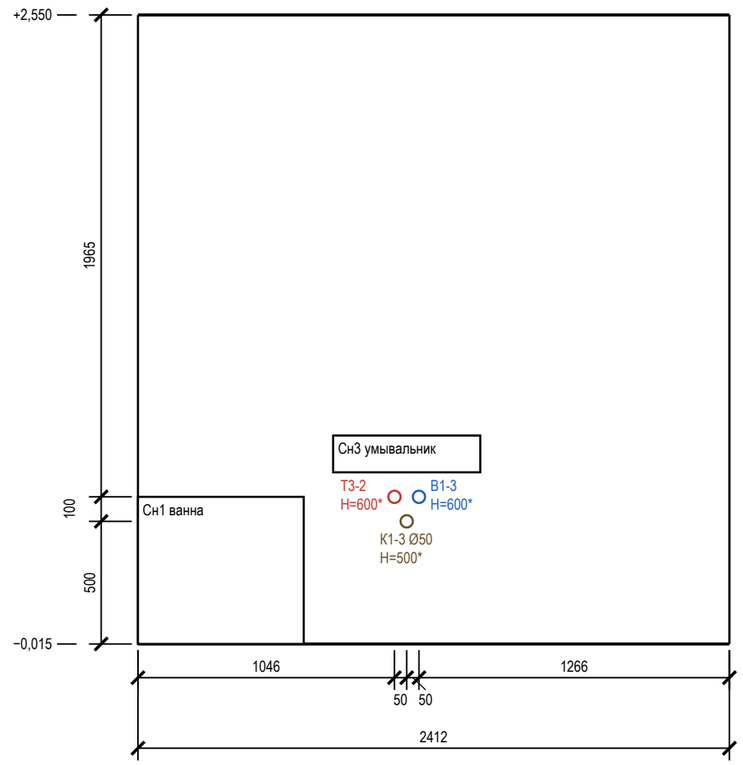

Ведомость привязок выводов (от чистого пола и угла)

Код	Прибор	Ø	H, мм	Привязка, мм
В1-2	Сн2 унитаз подвесной	½"	250*	ст. Б: 566 от лев. угла
К1-2	Сн2 унитаз подвесной	Ø110	220*	ст. Б: 416 от лев. угла
В1-1	Сн1 ванна	½"	800*	ст. В: 876 от лев. угла
Т3-1	Сн1 ванна	½"	800*	ст. В: 726 от лев. угла
К1-1	Сн1 ванна	Ø50	50*	ст. В: 1401 от лев. угла
В1-3	Сн3 умывальник	½"	600*	ст. Г: 1146 от лев. угла
Т3-2	Сн3 умывальник	½"	600*	ст. Г: 1046 от лев. угла
К1-3	Сн3 умывальник	Ø50	500*	ст. Г: 1096 от лев. угла

Условные обозначения

- вывод В1 (код — в ведомости привязок)
- вывод Т3 (код — в ведомости привязок)
- вывод К1 (код — в ведомости привязок)
- сантехприбор по расстановке (габарит модели)
- дверной проём; окно — сплошной контур

Допущения и предложения на листе

Основа листа: размеры сняты со скана обмерного плана KV design (см): часть подписей не читается, помещения выровнены по читаемым размерам; контрольный обмер не выполнен (К-1); высота потолка 2650 мм принята по отметкам обмера (Н = 2,50…2,66 м, ригель 2,28 м) — уточнить при обмере (К-2); толщины стен 300 / 120 мм приняты, межквартирная стена и колонны — по скану, не замерены (К-1); разрешённая мощность 15 кВт принята по типовым ТУ; при объединении двух квартир — переоформление ТУ (К-4); подрайон климата не задан — принят не северный (жилые от 2,5 м) (К-8). См. лист открытых вопросов (лист 6, записи К-1, К-2, К-4, К-8).

Примечания

1. Габариты и высоты приборов, межосевые смесителей и места кранов — по паспортам выбранных приборов, сверяются до разметки стен.
2. Высоты Н — от чистого пола помещения, мм; отметка чистого пола и потолка — у левого края вида (от ±0,000 объекта). Привязки — от левого чистового угла вида (облицовка стен вычтена), как на развёртках стен.
3. * — высота принята по практике монтажа: в данных прибора её нет; до разметки стен сверить по паспорту выбранного прибора (смеситель, инсталляция, сифон).
4. Стояки в помещении: Ст К1-1 Ø110, Ст В1-1 Ø32, Ст Т3-1 Ø32 — положение на плане выводов; выводы подключаются к ним по схеме разводки.
5. Ревизионные люки к арматуре и ревизиям в данных не заданы: место и размер не определены (записи реестра нет).
6. Часть подписей выводов не уместилась у знака: коды и высоты — в ведомости привязок.
7. Расчёт систем водоснабжения и канализации и подбор оборудования выполняет проектная организация; лист задаёт места и высоты выводов.

1000 мм · печать 1:1

Изм.	Кол.уч	Лист	№ док.	Подп.	Дата
Разраб.		Кырлан А.С.			04.11.26
Пров.					
ГИП					
Н. контр.					
Утв.					

ГД-2026-009-АИ

Квартира 103 м²

Общая площадь 100,72* м² · * размеры со скана, не замерены (реестр — л. 6, 7, К-1)

Дизайн-проект интерьера

Стадия	Лист	Листов
РП	39	120

Развёртки мокрых зон: выводы ВК. Ванная

М 1:25

Кырлан Александр Сергеевич


выпуск 04.11.2026 № 20cec94f32 · стр. 44 из 130

Развёртки мокрых зон: выводы ВК. Постирочная


пом. 7 · выводы В1, Т3, К1 на стенах · высоты от чистого пола, привязки от чистовых углов, мм

ПРЕДВАРИТЕЛЬНО · не для производства работ · открыто пунктов: 8 (реестр — л. 6, 7)

Стена А (М 1:20)

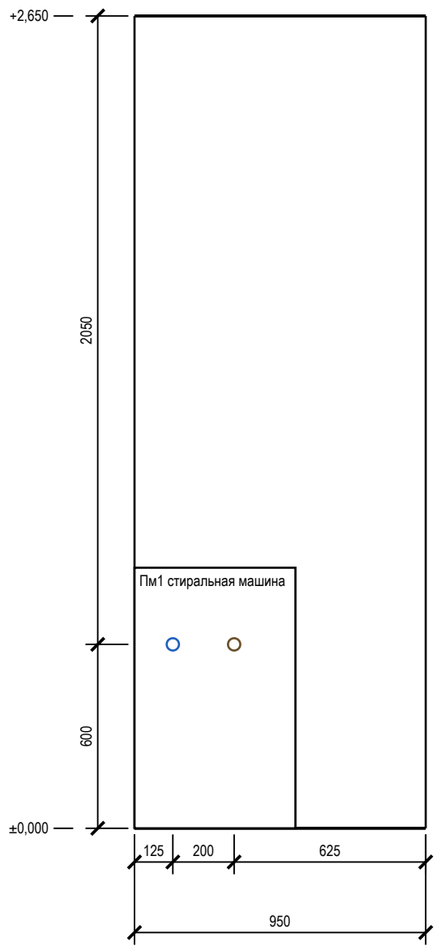

Стена Г (М 1:20)

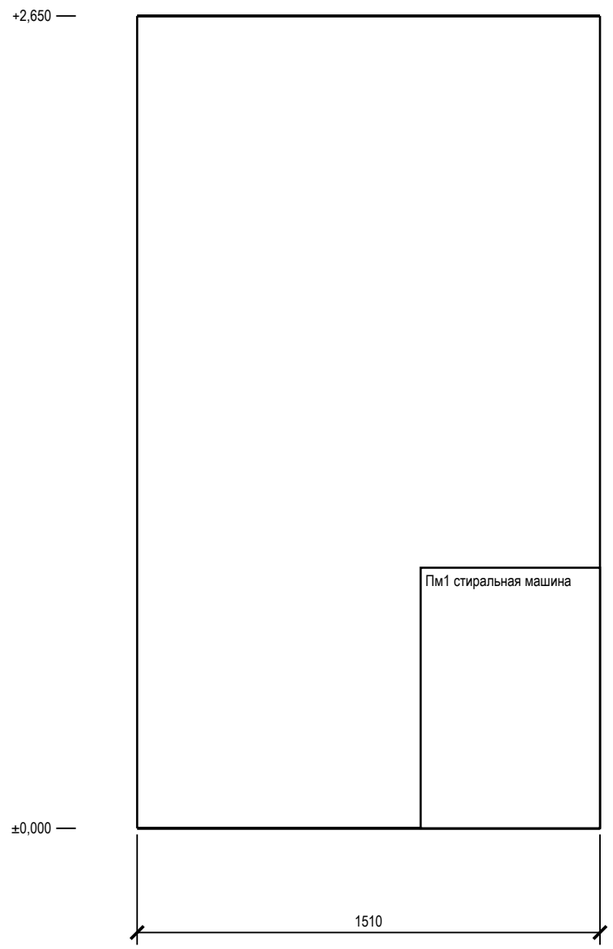

Допущения и предложения на листе

Основа листа: размеры сняты со скана обмерного плана KV design (см): часть подписей не читается, помещения выровнены по читаемым размерам; контрольный обмер не выполнен (К-1); высота потолка 2650 мм принята по отметкам обмера (Н = 2,50…2,66 м, ригель 2,28 м) — уточнить при обмере (К-2); толщины стен 300 / 120 мм приняты, межквартирная стена и колонны — по скану, не замерены (К-1); разрешённая мощность 15 кВт принята по типовым ТУ; при объединении двух квартир — переоформление ТУ (К-4); подрайон климата не задан — принят не северный (жилые от 2,5 м) (К-8).

См. лист открытых вопросов (лист 6, записи К-1, К-2, К-4, К-8).

Ведомость привязок выводов (от чистого пола и угла)

Код	Прибор	Ø	Н, мм	Привязка, мм
В1-4	Пм1 стиральная машина	½"	600*	ст. А: 125 от лев. угла
К1-4	Пм1 стиральная машина	Ø50	600*	ст. А: 325 от лев. угла

Условные обозначения

- вывод В1 (код — в ведомости привязок)
- вывод Т3 (код — в ведомости привязок)
- вывод К1 (код — в ведомости привязок)
- сантехприбор по расстановке (габарит модели)
- дверной проём; окно — сплошной контур

Примечания

1. Габариты и высоты приборов, межосевые смесителей и места кранов — по паспортам выбранных приборов, сверяются до разметки стен.
2. Высоты Н — от чистого пола помещения, мм; отметка чистого пола и потолка — у левого края вида (от ±0,000 объекта). Привязки — от левого чистового угла вида (облицовка стен вычтена), как на развёртках стен.
3. * — высота принята по практике монтажа: в данных прибора её нет; до разметки стен сверить по паспорту выбранного прибора (смеситель, инсталляция, сифон).
4. Стояки в помещении: Ст К1-4 (постирочная) Ø50, Ст В1-4 Ø32, Ст Т3-4 Ø32 — положение на плане выводов; выводы подключаются к ним по схеме разводки.
5. Ревизионные люки к арматуре и ревизиям в данных не заданы: место и размер не определены (записи реестра нет).
6. Часть подписей выводов не уместилась у знака: коды и высоты — в ведомости привязок.
7. Расчёт систем водоснабжения и канализации и подбор оборудования выполняет проектная организация; лист задаёт места и высоты выводов.

1000 мм · печать 1:1

Изм.	Кол.уч	Лист	№ док.	Подп.	Дата
Разраб.		Кырлан А.С.			04.11.26
Пров.					
ГИП					
Н. контр.					
Утв.					

ГД-2026-009-АИ

Квартира 103 м²

Общая площадь 100,72* м² · * размеры со скана, не замерены (реестр — л. 6, 7, К-1)

Дизайн-проект интерьера

Стадия	Лист	Листов
РП	40	120

Развёртки мокрых зон: выводы ВК. Постирочная

М 1:20

Кырлан Александр Сергеевич


выпуск 04.11.2026 № 20cec94f32 · стр. 45 из 130

Развёртки мокрых зон: выводы ВК. Ванная мастер


пом. 11 · выводы В1, Т3, К1 на стенах · высоты от чистого пола, привязки от чистовых углов, мм

ПРЕДВАРИТЕЛЬНО · не для производства работ · открыто пунктов: 8 (реестр — л. 6, 7)


Стена А (М 1:20)

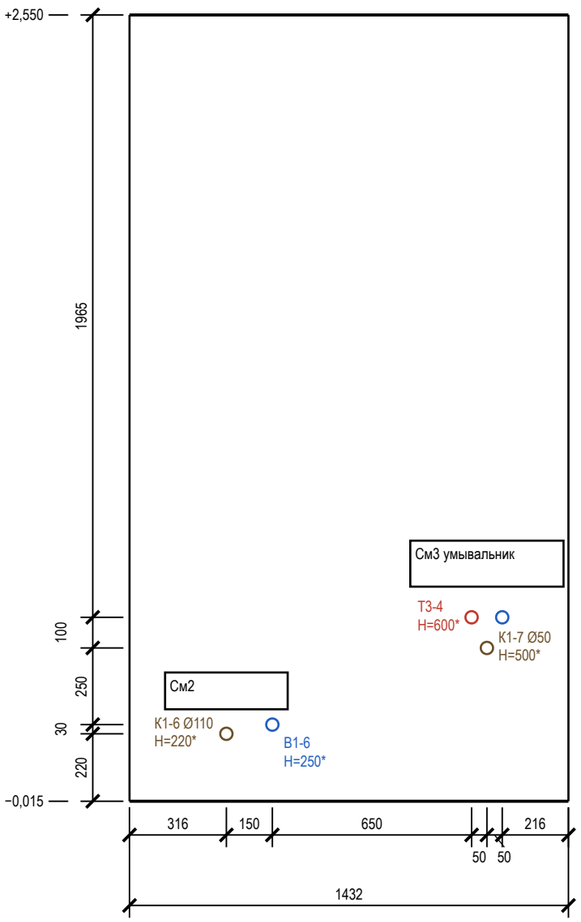

Стена Б (М 1:20)

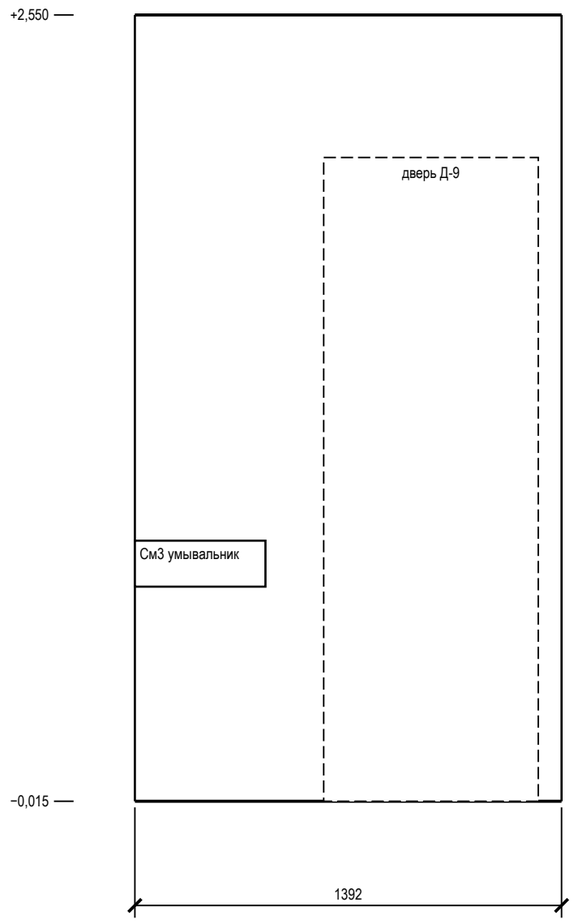

Стена В (М 1:20)

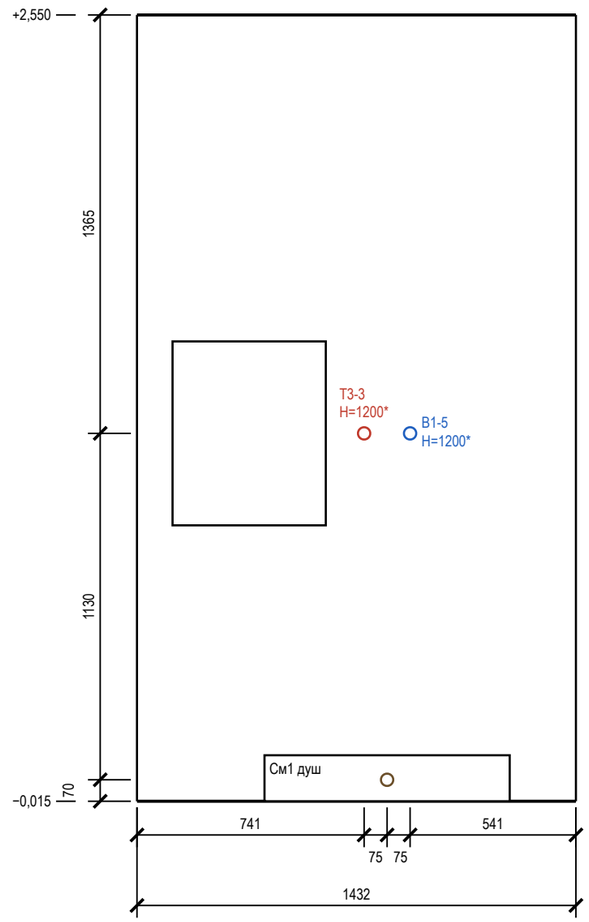

Допущения и предложения на листе

Основа листа: размеры сняты со скана обмерного плана KV design (см): часть подписей не читается, помещения выровнены по читаемым размерам; контрольный обмер не выполнен (К-1); высота потолка 2650 мм принята по отметкам обмера (Н = 2,50…2,66 м, ригель 2,28 м) — уточнить при обмере (К-2); толщины стен 300 / 120 мм приняты, межквартирная стена и колонны — по скану, не замерены (К-1); разрешённая мощность 15 кВт принята по типовым ТУ; при объединении двух квартир — переоформление ТУ (К-4); подрайон климата не задан — принят не северный (жилые от 2,5 м) (К-8).

Знак «*» — принято, не замерено и не подтверждено (замерить на объекте): К-6: Ст К1-3, Ст В1-3, Ст Т3-3 — положение снято со скана обмера, отдельно не замерялось; ось внутри габарита поддона См1 — обмер угла по К-6.

См. лист открытых вопросов (лист 6, записи К-1, К-2, К-4, К-6, К-8).

Ведомость привязок выводов (от чистого пола и угла)

Код	Прибор	Ø	Н, мм	Привязка, мм
В1-6	См2 унитаз подвесной	½"	250*	ст. А: 466 от лев. угла
К1-6	См2 унитаз подвесной	Ø110	220*	ст. А: 316 от лев. угла
В1-7	См3 умывальник	½"	600*	ст. А: 1216 от лев. угла
Т3-4	См3 умывальник	½"	600*	ст. А: 1116 от лев. угла

Ведомость привязок (продолжение)

Код	Прибор	Ø	Н, мм	Привязка, мм
К1-7	См3 умывальник	Ø50	500*	ст. А: 1166 от лев. угла
В1-5	См1 душ	½"	1200*	ст. В: 891 от лев. угла
Т3-3	См1 душ	½"	1200*	ст. В: 741 от лев. угла
К1-5	См1 душ	Ø50	70*	ст. В: 816 от лев. угла

Условные обозначения

- вывод В1 (код — в ведомости привязок)
- вывод Т3 (код — в ведомости привязок)
- вывод К1 (код — в ведомости привязок)
- сантехприбор по расстановке (габарит модели)
- дверной проём; окно — сплошной контур

Примечания

1. Габариты и высоты приборов, межосевые смесителей и места кранов — по паспортам выбранных приборов, сверяются до разметки стен.
2. Высоты Н — от чистого пола помещения, мм; отметка чистого пола и потолка — у левого края вида (от ±0,000 объекта). Привязки — от левого чистового угла вида (облицовка стен вычтена), как на развёртках стен.
3. * — высота принята по практике монтажа: в данных прибора её нет; до разметки стен сверить по паспорту выбранного прибора (смеситель, инсталляция, сифон).
4. Стояки в помещении: Ст К1-3* Ø110, Ст В1-3* Ø32, Ст Т3-3* Ø32 — положение на плане выводов; выводы подключаются к ним по схеме разводки.
5. Ревизионные люки к арматуре и ревизиям в данных не заданы: место и размер не определены (записи реестра нет).
6. Часть подписей выводов не уместилась у знака: коды и высоты — в ведомости привязок.
7. Расчёт систем водоснабжения и канализации и подбор оборудования выполняет проектная организация; лист задаёт места и высоты выводов.

1000 мм · печать 1:1

Изм.	Кол.уч	Лист	№ док.	Подп.	Дата
Разраб.		Кырлан А.С.			04.11.26
Пров.					
ГИП					
Н. контр.					
Утв.					

ГД-2026-009-АИ

Квартира 103 м²

Общая площадь 100,72* м² · * размеры со скана, не замерены (реестр — л. 6, 7, К-1)

Дизайн-проект интерьера

Стадия	Лист	Листов
РП	41	120

Развёртки мокрых зон: выводы ВК. Ванная мастер

М 1:20

Кырлан Александр Сергеевич

выпуск 04.11.2026 № 20cec94f32 · стр. 46 из 130

Спецификация сантехнического оборудования

Форма 1 ГОСТ 21.110-2013 · ГД-2026-009-АИ-ВК.СО · приборы, арматура, трубопроводы

ПРЕДВАРИТЕЛЬНО · не для производства работ · открыто пунктов: 8 (реестр — л. 6, 7)

Поз.	Наименование и техническая характеристика	Тип, марка, обозначение документа	Код продукции	Поставщик	Ед. изм.	Кол.	Масса 1 ед., кг	Примечание
	Санитарные приборы							
1	Ванна встраиваемая акриловая 1600×700 мм, с каркасом, экраном и отверстием слив-перелив	аналог		выбор заказчика	шт	1		Сн1
2	Унитаз подвесной безободковый, с сиденьем микролифт, крепёж и звукоизолирующая прокладка	Jacob Delafon Struktura EDF102-00		выбор заказчика	шт	2		Сн2, См2
3	Инсталляция для подвесного унитаза: рама высотой 1120 мм, бачок, клавиша смыва (ось клавиши 1050 мм от чистого пола)	аналог		выбор заказчика	шт	2		Сн2, См2; короб ГКЛВ
4	Умывальник подвесной 600×450 мм, с отверстием под смеситель и переливом	аналог		выбор заказчика	шт	1		Сн3
5	Умывальник подвесной 500×450 мм, с отверстием под смеситель и переливом	аналог		выбор заказчика	шт	1		См3
6	Поддон душевой низкий 800×800 мм, с сифоном и выпуском Ø50, на ножках/подиуме	аналог		выбор заказчика	шт	1		См1
7	Мойка кухонная врезная / подстольная, с переливом, ориентир 700×480 мм — в модуле Кх1 шириной 800 мм, вырез по шаблону модели	аналог		с кухонной мебелью	шт	1		Кх1
8	Полотенцесушитель электрический, IP44, с терморегулятором	аналог		выбор заказчика	шт	2		Сн4, См4
	Смесители, сифоны и арматура приборов							
9	Смеситель для ванны настенный однорычажный, межосевое 150 мм, с душевым набором (лейка, шланг, держатель)	аналог		выбор заказчика	шт	1		Сн1
10	Смеситель для умывальника однорычажный, с донным клапаном	аналог		выбор заказчика	шт	2		Сн3, См3
11	Душевая система скрытого монтажа с термостатом: встраиваемая часть, верхний душ, ручная лейка	аналог		выбор заказчика	шт	1		См1; встраиваемая часть — до плитки
12	Смеситель кухонный однорычажный, высокий излив	аналог		выбор заказчика	шт	1		Кх1
13	Обвязка ванны слив-перелив Ø40/50 с сифоном	аналог		выбор заказчика	шт	1		Сн1
14	Сифон для умывальника бутылочный Ø32/40–50, с гофрой к выпуску	аналог		выбор заказчика	шт	2		Сн3, См3
15	Сифон для мойки Ø40/50	аналог		выбор заказчика	шт	1		Кх1
16	Сифон для посудомоечной машины с обратным клапаном, на выводе слива Ø40	аналог		выбор заказчика	шт	1		Кх2
17	Сифон для стиральной машины встраиваемый в стену Ø50, с обратным клапаном	аналог		выбор заказчика	шт	1		Пм1
18	Кран угловой ½"×½" с гибкой подводкой 40 см (умывальники, мойка)	аналог		выбор заказчика	шт	6		по 2 на прибор
19	Кран шаровой угловой ½"×¾" для подключения стиральной и посудомоечной машины	аналог		выбор заказчика	шт	2		Пм1, Кх2
	Трубопроводы							
20	Труба полипропиленовая PP-R PN20 Ø20×3,4 (В1)	ГОСТ 32415-2013		выбор заказчика	м	19	0,17	11,4 + 5,5 + 10 %
21	Труба PP-R, армированная стекловолокном, PN20 Ø20×2,8 (Т3)	ГОСТ 32415-2013		выбор заказчика	м	12	0,15	6,9 + 3,8 + 10 %
22	Труба канализационная ПП Ø40 (К1)	ГОСТ 32414-2013		выбор заказчика	м	1		0,3 + 0,6 + 10 %
23	Труба канализационная ПП Ø50 (К1)	ГОСТ 32414-2013		выбор заказчика	м	8,5		5,6 + 2,1 + 10 %
24	Труба канализационная ПП Ø110 (К1)	ГОСТ 32414-2013		выбор заказчика	м	4,5		3,5 + 0,4 + 10 %
	Фасонные части и выводы							
25	Отвод канализационный ПП 45° Ø40	ГОСТ 32414-2013		выбор заказчика	шт	2		2 шт. на поворот
26	Отвод канализационный ПП 45° Ø50	ГОСТ 32414-2013		выбор заказчика	шт	24		2 шт. на поворот
27	Отвод канализационный ПП 45° Ø110	ГОСТ 32414-2013		выбор заказчика	шт	12		2 шт. на поворот
28	Тройник канализационный ПП 45° (врезки ветвей)	ГОСТ 32414-2013		выбор заказчика	шт	8		
29	Ревизия канализационная ПП (после поворота трассы)	ГОСТ 32414-2013		выбор заказчика	шт	11		доступ сохранить
30	Фитинги PP-R Ø20: тройники, угольники 90° (ветви и повороты В1, Т3)	ГОСТ 32415-2013		выбор заказчика	шт	42		
31	Водорозетка PP-R Ø20×½" настенная, с креплением	ГОСТ 32415-2013		выбор заказчика	шт	14		коды — лист выводов
	Узлы ввода, люки, короба							
32	Кран шаровой латунный Ду15 PN16 (отключение ввода)	аналог		выбор заказчика	шт	8		Ст В1-1, Ст Т3-1, Ст В1-2, Ст Т3-2, Ст В1-3*, Ст Т3-3*, Ст В1-4, Ст Т3-4
33	Фильтр сетчатый косой Ду15	аналог		выбор заказчика	шт	8		
34	Счётчик воды крыльчатый Ду15 (ХВ, ГВ), с поверкой	аналог		выбор заказчика	шт	8		пломба УК
35	Клапан обратный Ду15	аналог		выбор заказчика	шт	8		
36	Люк ревизионный нажимной под плитку 300×400 мм	аналог		выбор заказчика	шт	4		к стоякам и арматуре
37	Звукоизоляция стояка К1 в коробе: рулонный звукоизоляционный материал ≥ 10 мм, обмотка стояка на высоту этажа	аналог		выбор заказчика	м	10,8		Ст К1-1, Ст К1-2 (кухня), Ст К1-3*, Ст К1-4 (постирочная)
38	Короб К1 над полом: профиль ПН/ПС, ГКЛВ 12,5 мм под плитку	аналог		выбор заказчика	м	7,8		сечение — лист разводки

Примечания

1. Форма 1 ГОСТ 21.110-2013, ширины граф изменены по п. 4.1. «Аналог» — аналог по характеристикам: модели внести до черновых работ, привязки выводов сверить по паспортам.
2. Бытовая техника не входит (показана арматура подключения), мойка — в комплекте кухни (марка — модуля кухни, как у столяра). Длины труб — трасса листа разводки + подъёмы + 10 %.
3. Стояк К1 в коробе — звукоизоляция стояка в коробе без жёсткого контакта короба с трубой. Стояки со «*» (Ст К1-3*, Ст В1-3*, Ст Т3-3*) приняты положение и число узлов ввода сверить на объекте.
4. Расчёт систем водоснабжения и канализации, диаметры магистралей и подбор оборудования выполняет проектная организация.

Допущения и предложения на листе

Основа листа: размеры сняты со скана обмерного плана KV design (см): часть подписей не читается, помещения выровнены по читаемым размерам; контрольный обмер не выполнен (К-1); высота потолка 2650 мм принята по отметкам обмера (Н = 2,50…2,66 м, ригель 2,28 м) — уточнить при обмере (К-2); толщины стен 300 / 120 мм приняты, межквартирная стена и колонны — по скану, не замерены (К-1); разрешённая мощность 15 кВт принята по типовым ТУ; при объединении двух квартир — переоформление ТУ (К-4); подрайон климата не задан — принят не северный (жилые от 2,5 м) (К-8).

Знак «*» — принято, не замерено и не подтверждено (замерить на объекте): К-6: Ст К1-3, Ст В1-3, Ст Т3-3 — положение снято со скана обмера, отдельно не замерялось; ось внутри габарита поддона См1 — обмер угла по К-6.

См. лист открытых вопросов (лист 6, записи К-1, К-2, К-4, К-6, К-8).

Изм.	Кол.уч	Лист	№ док.	Подп.	Дата
Разраб.		Кырлан А.С.			04.11.26
Пров.					
ГИП					
Н. контр.					
Утв.					

ГД-2026-009-АИ

Квартира 103 м²

Общая площадь 100,72* м² · * размеры со скана, не замерены (реестр — л. 6, 7, К-1)

Дизайн-проект интерьера	Стадия	Лист	Листов
	РП	42	120

Спецификация сантехнического оборудования

М б/м

Кырлан Александр Сергеевич

выпуск 04.11.2026 № 20cec94f32 · стр. 47 из 130

Техническое задание на подбор светильников

ПРЕДВАРИТЕЛЬНО · не для производства работ · открыто пунктов: 8 (реестр — л. 6, 7)

Параметры для подбора: светильники, ленты и блоки питания, сценарии помещений со светорегуляторами · б/м

Параметры светильников для подбора

Поз.	Марки	Наименование	Установка	Кол.	P, Вт	Σ P, Вт	Ф, лм	Тц, К	Ra	Угол, °	IP	Дим.	Слой	Группа	Пом.
1	Св17–Св22, Св56–Св61	Встраиваемый точечный	в ГКЛ, корпус ≤ 70 мм	12	12	144	1050	2700	90	—	20	—	общий	L7, L15	1, 8
2	Св23**, Св62**	Лента светодиодная 24 В	на поверхности, профиль с рассеивателем	24,6 м	9,6/м	236,2	900/м	2700	90	—	20	да	акцентный	L8, L16	1, 8
3	Св16, Св55	Потолочный накладной	на потолке, засветка стены	2	10	20	900	3000	90	—	20	—	общий	L6, L14	2, 7
4	Св1–Св8, Св31–Св37	Встраиваемый точечный	в ГКЛ, корпус ≤ 70 мм	15	12	180	1000	3000	90	—	20	—	общий	L1, L4	3, 5
5	Св9	Подвесной	подвес, низ H=1600	1	15	15	1200	2700	90	—	20	—	рабочий	L2	3
6	Св10**	Лента светодиодная 24 В	на поверхности, профиль с рассеивателем	5,4 м	9,6/м	51,8	900/м	2700	90	—	20	да	акцентный	L3	3
7	Св26–Св29, Св53, Св54	Встраиваемый точечный	в ГКЛ, корпус ≤ 70 мм	6	7	42	600	3000	90	—	20	—	общий	L10	4, 9
8	Св30**	Лента светодиодная 24 В	на поверхности, профиль с рассеивателем, датчик движения	1,8 м	4,8/м	8,6	150/м	2700	90	—	20	нет	ночной	L11	4
9	Св38, Св39	Линейный светильник	на поверхности	1,2 м	8	16	700	3000	90	—	20	—	рабочий	L5	5
10	Св12–Св14, Св51	Встраиваемый точечный	в ГКЛ, корпус ≤ 70 мм	4	6	24	500	3000	90	—	44	—	общий	L12, L17	6, 11
11	Св15**, Св52**	Настенный светильник над зеркалом, драйвер встроен	над зеркалом, H=1900	2	8	16	600	3000	90	—	44	—	рабочий	L13, L18	6, 11
12	Св11, Св64, Св74	Настенный (бра)	на стене, H=1500	3	6	18	400	2700	90	60	20	—	рабочий	L19, L22	8, 10
13	Св65–Св72	Встраиваемый точечный	в ГКЛ, корпус ≤ 70 мм	8	12	96	1000	2700	90	—	20	—	общий	L20	10
14	Св73**	Лента светодиодная 24 В	на поверхности, профиль с рассеивателем	15,5 м	9,6/м	148,8	900/м	2700	90	—	20	да	акцентный	L21	10
15	Св50	Встраиваемый точечный	в ГКЛ, корпус ≤ 70 мм	1	7	7	600	3000	90	—	44	—	общий	L17	11
		Итого		**54 шт + 48,5 м**		**1023,4**									

LED-ленты, линейные светильники и блоки питания

Марка	Пом.	L, м	U, В	Вт/м	Σ P, Вт	БП	P БП, Вт	Загр., %	Питание	Доступ к БП
Св23**	1	12,3	24	9,6	118,1	БП2	200	59	с двух концов	люк 300×300 в коробе У1 у окна
Св10**	3	5,4	24	9,6	51,8	БП1	100	52	с одного конца	люк 300×300 в коробе потолка у стены А
Св30**	4	1,8	24	4,8	8,6	БП3	20	43	с одного конца	в шкафу П1, верхняя полка
Св38	5	0,6	24	—	8	БП4	30	53	встроенный ввод	в колонне Кх5 над холодильником, съёмная панель
Св39	5	0,6	24	—	8	БП4	30	53	встроенный ввод	в колонне Кх5 над холодильником, съёмная панель
Св62**	8	12,3	24	9,6	118,1	БП5	200	59	с двух концов	люк 300×300 в коробе У1 у окна
Св73**	10	15,5	24	9,6	148,8	БП6	200	74	с двух концов	люк 300×300 в коробе У1 у входа

Сценарии (помещения со светорегуляторами)

Помещение	Сценарий	Горят группы (уровень)	Управление
3. Гостиная-столовая	Вечер	L2 подвес над обеденным столом — вкл.; L3 лента в карнизе (диммер) — 50 %; остальные выкл.	светорегулятор S2**; выключатель S1
	Гости	L1 общий свет (споты) — вкл.; L2 подвес над обеденным столом — вкл.; L3 лента в карнизе (диммер) — 100 %	светорегулятор S2**; выключатель S1
	Кино	L3 лента в карнизе (диммер) — 20 %; остальные выкл.	светорегулятор S2**
	Уборка	L1 общий свет (споты) — вкл.; L2 подвес над обеденным столом — вкл.; остальные выкл.	выключатель S1

Допущения и предложения на листе

Основа листа: размеры сняты со скана обмерного плана KV design (см): часть подписей не читается, помещения выровнены по читаемым размерам; контрольный обмер не выполнен (К-1); высота потолка 2650 мм принята по отметкам обмера (H = 2,50…2,66 м, ригель 2,28 м) — уточнить при обмере (К-2); толщины стен 300 / 120 мм приняты, межквартирная стена и колонны — по скану, не замерены (К-1); разрешённая мощность 15 кВт принята по типовым ТУ; при объединении двух квартир — переоформление ТУ (К-4); подрайон климата не задан — принят не северный (жилые от 2,5 м) (К-8).

Знак «**» — предложение проектировщика, заказчиком не утверждено (согласовать с заказчиком): Св23, Св10, Св30, Св62, Св73 — открытая лента в накладном профиле вместо «в коробе»: короба в потолке нет — высота 2650 мм < 2700 — один уровень (табл. 1.3); S2 — светорегулятор добавлен под диммируемую ленту L3; уровни сценариев выбраны конвейером; Св15 — Сдвиг под раскладку плитки стены Г на 141 мм вдоль стены — ось на шве или в центре плитки, привязка по таблице листа; Св52 — свет у зеркала — над зеркалом у умывальника по его оси (свет на лицо, а не над сантехникой); сдвиг под раскладку плитки стены А на 149 мм вдоль стены — ось на шве или в центре плитки, привязка по таблице листа.

См. лист открытых вопросов (лист 6, записи К-1, К-2, К-4, К-8).

Примечания

1. Позиции и марки Св — те же, что на плане освещения (лист 24) и в ведомости светильников (лист 26); группы L — по плану выключателей (лист 25).
2. Модели светильников не выбраны: лист — техническое задание на подбор. Модель по строке таблицы: поток, Тц, Ra, угол, IP и регулировка яркости не хуже указанных, мощность не больше; встраиваемые — под глубину короба (графа «Установка»). IP 20 — сухие помещения. После выбора моделей (артикул, производитель) лист выпускается как «Спецификация светильников».
3. Длина LED-ленты в карнизе — по линии карниза плана потолков (лист 45); Σ P = Вт/м × длина. Блок питания загружен не больше чем на 80 %; лента 24 В длиннее 10 м питается с двух концов; доступ к блоку питания — люк ревизии 300×300 мм или место, указанное в таблице.
4. Сценарии: % — яркость группы на светорегуляторе; «вкл.» — группа на обычной клавише; группы, не названные в строке, выключены. Светильники и блоки питания групп на светорегуляторе — с регулировкой яркости. Клавиши и светорегуляторы — лист 25.
5. В пом. 1, 8, 10 свет включается клавишами групп — лист 25.
6. Мощность и поток в таблице — требования к подбору (поток не меньше, мощность не больше указанных); после выбора модели — по её паспорту, Σ P — установленная мощность освещения. Оценка освещённости — на плане освещения; это не светотехнический расчёт.
7. Окончание: «Слои света по помещениям» — лист 44.

Изм.	Кол.уч	Лист	№ док.	Подп.	Дата
Разраб.		Кырлан А.С.			04.11.26
Пров.					
ГИП					
Н. контр.					
Утв.					

ГД-2026-009-АИ

Квартира 103 м²

Общая площадь 100,72* м² · * размеры со скана, не замерены (реестр — л. 6, 7, К-1)

Дизайн-проект интерьера

Стадия	Лист	Листов
РП	43	120

Техническое задание на подбор светильников

М б/м

Кырлан Александр Сергеевич

выпуск 04.11.2026 № 20cec94f32 · стр. 48 из 130

Техническое задание на подбор светильников (продолжение)

Продолжение таблиц · б/м

Слои света по помещениям

Пом.	Помещение	Слои света — группы включения (марки — в спецификации)	Σ P, Вт
1	Кабинет-библиотека	общий — L7; акцентный — L8	190,1
2	Кладовая	общий — L6	10
3	Гостиная-столовая	общий — L1; рабочий — L2; акцентный — L3	162,8
4	Прихожая-холл	общий — L10; ночной — L11	36,6
5	Кухня	общий — L4; рабочий — L5	100
6	Ванная	общий — L12; рабочий — L13	26
7	Постирочная	общий — L14	10
8	Спальня 2	общий — L15; рабочий — L19; акцентный — L16	196,1
9	Коридор	общий — L10	14
10	Спальня мастер	общий — L20; рабочий — L22; акцентный — L21	256,8
11	Ванная мастер	общий — L17; рабочий — L18	21

Слои света

общий — равномерный свет помещения, по норме освещённости

рабочий — местный свет задачи: столешница, зеркало, чтение у кровати

акцентный — подсветка потолка, стен и ниш; не входит в поток общего света

ночной — путь спальня → санузел: не выше 2700 K, малая яркость, датчик движения

Примечания

1. Продолжение листа 43: позиции, марки и группы — те же, что на основном листе.
2. Σ P — установленная мощность освещения помещения, Вт; группы L — по плану выключателей.

Допущения и предложения на листе

Основа листа: размеры сняты со скана обмерного плана KV design (см): часть подписей не читается, помещения выровнены по читаемым размерам; контрольный обмер не выполнен (К-1); высота потолка 2650 мм принята по отметкам обмера (H = 2,50…2,66 м, ригель 2,28 м) — уточнить при обмере (К-2); толщины стен 300 / 120 мм приняты, межквартирная стена и колонны — по скану, не замерены (К-1); разрешённая мощность 15 кВт принята по типовым ТУ; при объединении двух квартир — переоформление ТУ (К-4); подрайон климата не задан — принят не северный (жилые от 2,5 м) (К-8).

См. лист открытых вопросов (лист 6, записи К-1, К-2, К-4, К-8).

Изм.	Кол.уч	Лист	№ док.	Подп.	Дата
Разраб.		Кырлан А.С.			04.11.26
Пров.					
ГИП					
Н. контр.					
Утв.					

ГД-2026-009-АИ

Квартира 103 м²

Общая площадь 100,72* м² · * размеры со скана, не замерены (реестр — л. 6, 7, К-1)

Дизайн-проект интерьера

Стадия	Лист	Листов
РП	44	120

Техническое задание на подбор светильников (продолжение)

М б/м

Кырлан Александр Сергеевич

06

Потолки и ГКЛ-конструкции


Кырлан Александр Сергеевич

выпуск 04.11.2026 · 20cec94f32 · стр. 50 из 130

План потолков

Уровни и марки потолков, короба с подсветкой, ниши под шторы, люки, вырезы · отметки низа от ±0,000 чистого пола · размеры в мм

ПРЕДВАРИТЕЛЬНО · не для производства работ · открыто пунктов: 8 (реестр — л. 6, 7)

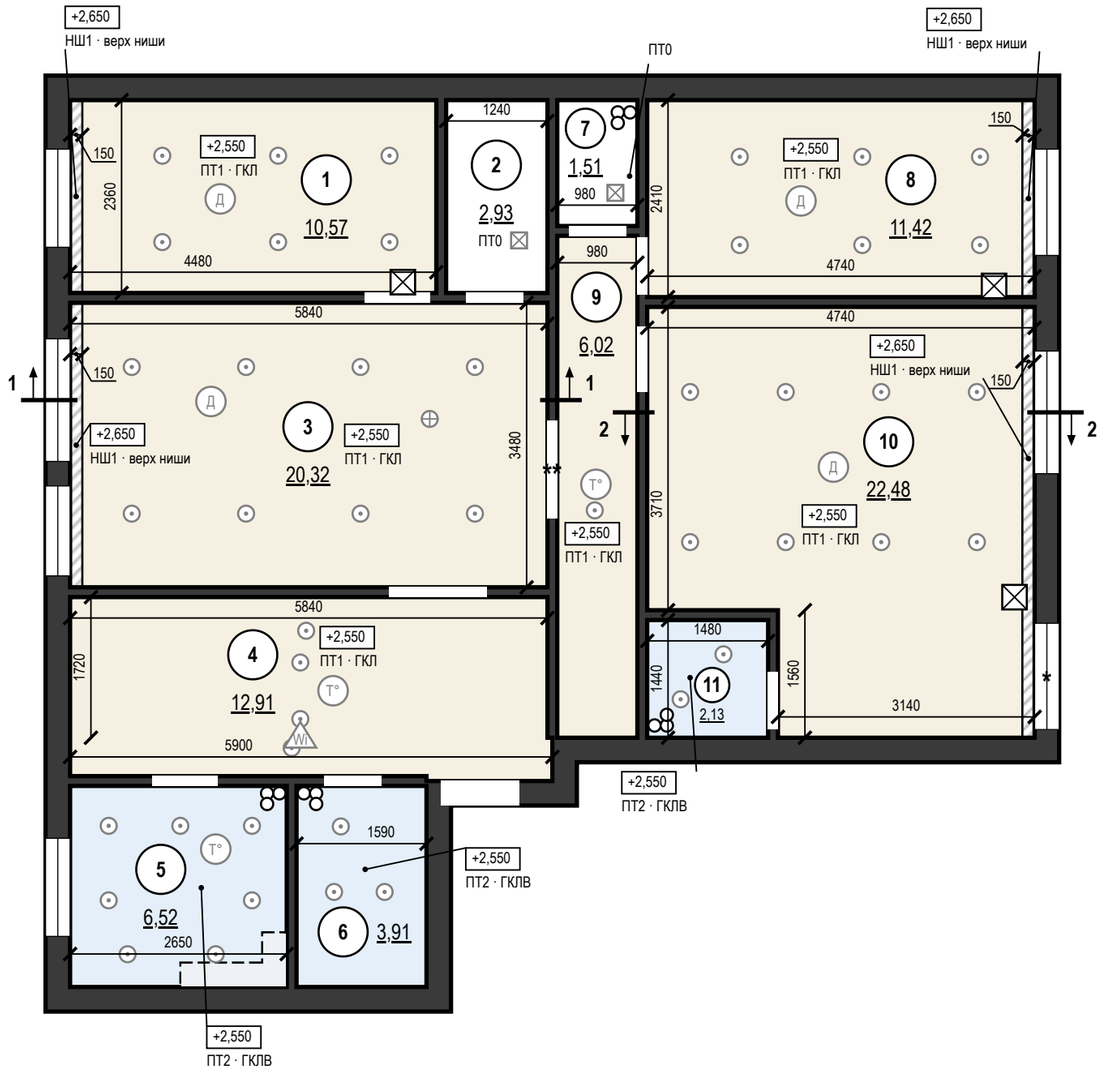

Условные обозначения

- ПТ1 — ГКЛ по каркасу П113, низ +2,550
- ПТ2 — ГКЛВ по каркасу П113, низ +2,550
- ПТ0 — существующий потолок, окраска, без подвесного потолка, низ +2,650
- НШ1 — ниша под шторы 150×100, верх +2,650
- граница уровней потолка (перепад)
- стояк: К1 — канализация, В1 — ХВС, Т3 — ГВС
- люк ревизии в потолке 300×300 мм (доступ к БП LED)
- светильник встраиваемый — подложка с плана освещения
- светильник накладной — подложка с плана освещения
- светильник подвесной — подложка с плана освещения
- Д — извещатель дымовой на потолке подложка
- Т° — извещатель тепловой на потолке подложка
- Wi — точка доступа Wi-Fi на потолке подложка
- короб воздуховода вытяжки ГКЛ (трасса — план вентиляции)
- линия разреза у стен помещения, стрелка — направление взгляда
- +2,600 — отметка низа потолка, м (у ниши под шторы — верх ниши); под ней марка потолка
- 1 — номер помещения, площадь м²

Ведомость потолков

Пом.	Марка	Конструкция	Низ / верх ниши	S, м²	Q
1	ПТ1	ГКЛ П113	+2,550	10,22	Q3
1	НШ1	ниша под шторы 150×100	+2,650	0,35	
2, 7	ПТ0	Существующий потолок, окраска	+2,650	4,44	
3	ПТ1	ГКЛ П113	+2,550	19,80	Q3
3	НШ1	ниша под шторы 150×100	+2,650	0,52	
4	ПТ1	ГКЛ П113	+2,550	12,91	Q3
5	ПТ2	ГКЛВ П113	+2,550	6,52	Q3
6	ПТ2	То же	+2,550	3,91	Q3
8	ПТ1	ГКЛ П113	+2,550	11,06	Q3
8	НШ1	ниша под шторы 150×100	+2,650	0,36	
9	ПТ1	ГКЛ П113	+2,550	6,02	Q3
10	ПТ1	То же	+2,550	21,69	Q3
10	НШ1	ниша под шторы 150×100	+2,650	0,79	
11	ПТ2	ГКЛВ П113	+2,550	2,13	Q3
		Итого		**100,72**	

Ведомость вырезов и закладных в потолке

Марка	Устройство	Кол.	Пом.
	Светильник встраиваемый (марки — план освещения)	46	1, 3, 4, 5, 6, 8, 9, 10, 11
	Светильник накладной (марки — план освещения)	2	2, 7
	Светильник подвесной (марки — план освещения)	1	3
ИП2, ИП1, ИП7, ИП8	Извещатель дымовой	4	1, 3, 8, 10
ИП3, ИП4, ИП6	Извещатель тепловой	3	4, 5, 9
АР1**	Точка доступа Wi-Fi, PoE	1	4
	Люк ревизии 300×300	3	1, 8, 10

Допущения и предложения на листе

Основа листа: размеры сняты со скана обмерного плана KV design (см): часть подписей не читается, помещения выровнены по читаемым размерам; контрольный обмер не выполнен (К-1); высота потолка 2650 мм принята по отметкам обмера (Н = 2,50…2,66 м, ригель 2,28 м) — уточнить при обмере (К-2); толщины стен 300 / 120 мм приняты, межквартирная стена и колонны — по скану, не замерены (К-1); разрешённая мощность 15 кВт принята по типовым ТУ; при объединении двух квартир — переоформление ТУ (К-4); подрайон климата не задан — принят не северный (жилые от 2,5 м) (К-8).

Знак «*» — принято, не замерено и не подтверждено (замерить на объекте): К-1: окно пом. 10 (стена Б) — Окно 1300 при offset 3500 на стене Б основной части (длина 3830) выходило за стену на 970 мм; К-6: Ст К1-3, Ст В1-3, Ст Т3-3 — положение снято со скана обмера, отдельно не замерялось; ось внутри габарита поддона См1 — обмер угла по К-6.

Знак «**» — предложение проектировщика, заказчиком не утверждено (согласовать с заказчиком): АР1 — точка доступа Wi-Fi: число и места; К-5: дверь пом. 3 (стена Б) — проём в межквартирной стене — объединение квартир, предложение до техзаключения.

Открытые вопросы и конфликты по листу: К-2, К-8.

См. лист открытых вопросов (лист 6, записи К-1, К-2, К-4–К-6, К-8).

Примечания

1. За отметку ±0,000 принят уровень чистого пола сухих помещений (готовое покрытие), а не существующего пола; пол пом. 6, 11 — −0,015; верх плиты перекрытия −0,064 — расчётный по пирогу пола, не замерен; существующий пол снимается до плиты, его отметка не замерена. Отметки в прямоугольниках — низ потолка; низ перекрытия +2,650. Марка потолка — одна конструкция и отметка на весь альбом.
2. Размеры помещений в свету (ширина × длина, мм), не поместившиеся на плане: пом. 2 — 1240 × 2360; пом. 4 — 5840 × 1720, 5900 × 470, 1540 × 60; пом. 5 — 2650 × 2460; пом. 6 — 1590 × 2460; пом. 7 — 980 × 1540; пом. 9 — 980 × 6140.
3. Потолки ГКЛ — каркасная система П113: подвесы через 1000 (с запасом: СП 163, табл. 14 — до 1100 при 0,15 кН/м²), несущие профили через 500, основные через 1200 мм; листы — поперёк несущих профилей. В помещениях 5, 6, 11 — ГКЛВ на оцинкованном каркасе.
4. Ниши под шторы 150×100 мм — на всю длину стены с окном; карниз — на закладной до обшивки (узел 1, лист 46).
5. Примыкание к стенам: теневой шов 15 мм, техзазор 3 мм — пом. 1, 3, 4, 5, 8, 9, 10, по стенам, выровненным штукатуркой (узел 1); пом. 6, 11 — разделительная лента.
6. Светильники и потолочные устройства — подложка с планов освещения, слаботочных систем и вентиляции (положение — по ним); вырезы и закладные — по ведомости на листе, до обшивки; отверстия не совмещать с профилями, глубина корпуса светильника до 70 мм.
7. Разрезы 1–1, 2–2 — на листе 46; высоты мебели и дверных блоков сверены с низом потолка в разрезах.
8. Узлы по выноскам на плане: узел 1 — лист 46; сечения М 1:10 по помещениям — лист 48.
9. Шпаклевание ГКЛ и условия приёмки — Q3: рассеянный дневной свет, осмотр с 2 м; боковой свет не оценивается.
10. Пом. 5: короб воздуховода кухонной вытяжки ГКЛ 300×130 мм (ширина от стены × высота), низ +2,520, длина 1,37 м — по трассе плана вентиляции, вдоль стен до входа в канал; под плоский воздуховод 200×60 (сечение ≈ Ø125): круглый Ø125 в коробе 200 мм опустил бы кухню ниже 2,5 м — сечение подтверждает раздел ОВ; каркас ПН 28×27 по стене и плите, ПП 60×27, лист ГКЛ 12,5.
11. Люки ревизии 300×300 мм — по центру блоков питания LED (БП2, БП5, БП6; координаты — план освещения).
12. Сечения потолков М 1:10: пом. 1 — 1.1, 1.2 (лист 48); пом. 3 — 1.1, 1.2 (лист 48); пом. 8 — 1.1, 1.2 (лист 48); пом. 10 — 1.1, 1.2 (лист 48).

1000 мм · печать 1:1

Изм.	Кол.уч	Лист	№ док.	Подп.	Дата
Разраб.		Кырлан А.С.			04.11.26
Пров.					
ГИП					
Н. контр.					
Утв.					

ГД-2026-009-АИ

Квартира 103 м²

Общая площадь 100,72* м² · * размеры со скана, не замерены (реестр — л. 6, 7, К-1)

Дизайн-проект интерьера

Стадия	Лист	Листов
РП	45	120

План потолков

М 1:75

Кырлан Александр Сергеевич


выпуск 04.11.2026 № 20cec94f32 · стр. 51 из 130

Разрезы и узлы потолков

Разрезы по потолкам с отметками уровней · узлы коробов и ниш · размеры в мм


Разрез 1–1 (М 1:40)

Пом. 3 Гостиная-столовая; линия разреза — план потолков, лист 45

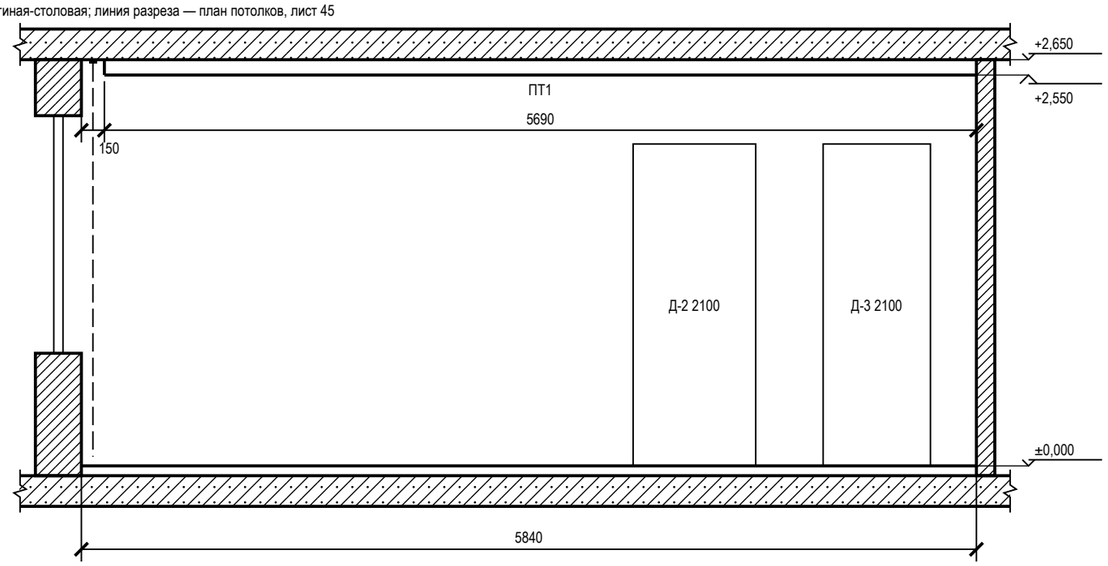


Разрез 2–2 (М 1:40)

Пом. 10 Спальня мастер; линия разреза — план потолков, лист 45

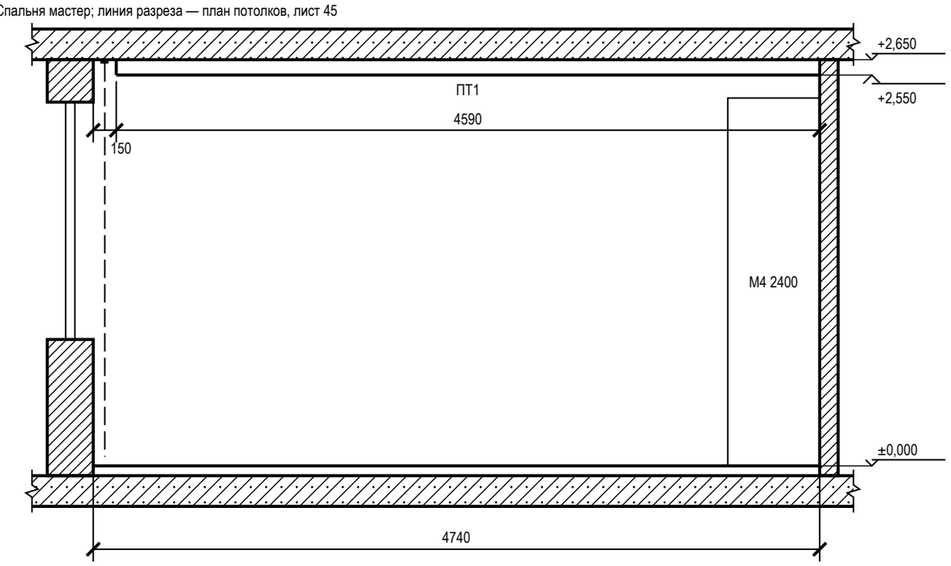

1 Ниша под шторы (М 1:10)

Пом. 1, 3, 8, 10; без подсветки; закладные под карниз — до обшивки

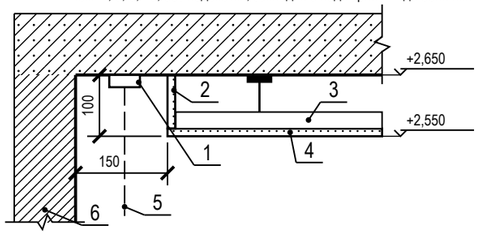

1 — карниз (шина), высота с верхом портьеры 80 мм
2 — стенка ниши — ГКЛ 12,5
3 — ПП 60×27 — каркас короба
4 — низ короба нижнего уровня — ГКЛ 12,5
5 — портьера
6 — стена с окном

Условные обозначения

- плита перекрытия в сечении
- стена в сечении
- потолок ГКЛ в сечении; под линией — марка потолка (план потолков)
- мебель и дверные проёмы за секущей плоскостью; число — марка и верх от чистого пола, мм
- портьера в нише под шторы

Допущения и предложения на листе

Основа листа: размеры сняты со скана обмерного плана KV design (см): часть подписей не читается, помещения выровнены по читаемым размерам; контрольный обмер не выполнен (К-1); высота потолка 2650 мм принята по отметкам обмера (Н = 2,50…2,66 м, ригель 2,28 м) — уточнить при обмере (К-2); толщины стен 300 / 120 мм приняты, межквартирная стена и колонны — по скану, не замерены (К-1); разрешённая мощность 15 кВт принята по типовым ТУ; при объединении двух квартир — переоформление ТУ (К-4); подрайон климата не задан — принят не северный (жилые от 2,5 м) (К-8).

См. лист открытых вопросов (лист 6, записи К-1, К-2, К-4, К-8).

Примечания

1. Разрезы — по линиям 1–1, 2–2 на плане потолков (лист 45). Отметки — от ±0,000 чистого пола, м; размеры — мм.
2. Высоты мебели и дверных блоков за секущей плоскостью сверены с низом потолка над ними: верх ниже низа короба и поля.
3. ГКЛ 12,5 мм по каркасу П113. Ниша под шторы — на всю длину стены с окном, карниз на закладной до обшивки (узел 1 — на этом листе).
4. Толщины плит перекрытия и пирога пола показаны условно.
5. Сечения потолков по помещениям М 1:10 (отметки помещения, профили, подвесы, крепёж, изделия) — лист 48.
6. Ведомость объёмов потолков (лист ГКЛ, профиль, подвесы, лента, блоки питания, люки) — на листе 47.

1000 мм · печать 1:1

Изм.	Кол.уч	Лист	№ док.	Подп.	Дата
Разраб.		Кырлан А.С.			04.11.26
Пров.					
ГИП					
Н. контр.					
Утв.					

ГД-2026-009-АИ

Квартира 103 м²

Общая площадь 100,72* м² · * размеры со скана, не замерены (реестр — л. 6, 7, К-1)

Дизайн-проект интерьера

Стадия	Лист	Листов
РП	46	120

Разрезы и узлы потолков

М 1:40; 1:10

Кырлан Александр Сергеевич

выпуск 04.11.2026 № 20cec94f32 · стр. 52 из 130

Разрезы и узлы потолков (продолжение)

Ведомость объёмов · размеры в мм

Ведомость объёмов потолков

Позиция	Ед.	Кол.	Пом.
Лист ГКЛ 12,5	м²	85,08	1, 3, 4, 8, 9, 10
Лист ГКЛВ 12,5	м²	12,56	5, 6, 11
Борта и карнизы (входят в площади листов выше)	м²	1,36	1, 3, 8, 10
Профиль ПП 60×27	м	276,03	1, 3, 4, 5, 6, 8, 9, 10, 11
Профиль ПН 28×27	м	148,38	1, 3, 4, 5, 6, 8, 9, 10, 11
Подвес прямой	шт.	84	1, 3, 4, 5, 6, 8, 9, 10, 11
Анкер-клин к плите	шт.	84	1, 3, 4, 5, 6, 8, 9, 10, 11
Шуруп TN 3,5×25	шт.	2246	1, 3, 4, 5, 6, 8, 9, 10, 11
Лента армирующая для швов	м	117,17	1, 3, 4, 5, 6, 8, 9, 10, 11
Шпаклёвка для швов	кг	39,06	1, 3, 4, 5, 6, 8, 9, 10, 11
Грунтовка (швы)	л	9,76	1, 3, 4, 5, 6, 8, 9, 10, 11
Лента разделительная по периметру	м	121,34	1, 3, 4, 5, 6, 8, 9, 10, 11
Сплошная шпаклёвка и окраска (площадь развёртки)	м²	97,64	1, 3, 4, 5, 6, 8, 9, 10, 11
Люк ревизии	шт.	3	1, 8, 10

Допущения и предложения на листе

Основа листа: размеры сняты со скана обмерного плана KV design (см): часть подписей не читается, помещения выровнены по читаемым размерам; контрольный обмер не выполнен (К-1); высота потолка 2650 мм принята по отметкам обмера (Н = 2,50…2,66 м, ригель 2,28 м) — уточнить при обмере (К-2); толщины стен 300 / 120 мм приняты, межквартирная стена и колонны — по скану, не замерены (К-1); разрешённая мощность 15 кВт принята по типовым ТУ; при объединении двух квартир — переоформление ТУ (К-4); подрайон климата не задан — принят не северный (жилые от 2,5 м) (К-8).

См. лист открытых вопросов (лист 6, записи К-1, К-2, К-4, К-8).

Примечания

1. ГКЛ 12,5 мм по каркасу П113; узлы коробов и ниш под шторы: узел 1 — лист 46; условные обозначения разрезов — на листе 46.
2. Ведомость объёмов — по геометрии плана потолков: Лист ГКЛ 12,5 — плоскости уровней + борта (без арочных участков); Лист ГКЛВ 12,5 — плоскости уровней + борта; Борта и карнизы — длина перепада × перепад; Профиль ПП 60×27 — S × (1/шаг несущ. + 1/шаг осн.) + стойки бортов; Профиль ПН 28×27 — периметр стен + 2 × перепады + карнизы; Подвес прямой — по раскладке: S уровня / (шаг осн. × шаг подвесов), пояс уже шага — ряд вдоль пояса, фигура — по контуру; шаг подвесов — не больше табл. 14 СП 163; Анкер-клин к плите — по одному на подвес (Knauf П113); Шуруп TN 3,5×25 — 23 шт./м² (Knauf П113, табл. 2 альбома П 11); Лента армирующая для швов — 1,2 м/м² листа (Knauf); Шпаклёвка для швов — 0,4 кг/м² листа, только швы (Knauf); Грунтовка (швы) — 0,1 л/м² листа, только швы (Knauf); Лента разделительная по периметру — периметр стен под потолком ГКЛ; Сплошная шпаклёвка и окраска (площадь развёртки) — плоскости + борта; расход — по паспорту материала (норма расхода на сплошной слой не подтверждена); Люк ревизии — план потолков; без запаса на подрезку (при закупке листа: ×1,075 при S > 20 м², ×1,175 — 10–20 м², ×1,275 — < 10 м²).

Изм.	Кол.уч	Лист	№ док.	Подп.	Дата
Разраб.		Кырлан А.С.			04.11.26
Пров.					
ГИП					
Н. контр.					
Утв.					

ГД-2026-009-АИ

Квартира 103 м²

Общая площадь 100,72* м² · * размеры со скана, не замерены (реестр — л. 6, 7, К-1)

Дизайн-проект интерьера

Стадия	Лист	Листов
РП	47	120

Разрезы и узлы потолков (продолжение)

М б/м

Кырлан Александр Сергеевич


выпуск 04.11.2026 № 20cec94f32 · стр. 53 из 130

Сечения потолков М 1:10

Пом. 1, 3, 8, 10 · профили, подвесы, крепёж, изделия · размеры в мм

Сечение 1.1. Ниша под шторы (М 1:10)

Пом. 1 Кабинет-библиотека, 3 Гостиная-столовая, 8 Спальня 2, 10 Спальня мастер; без подсветки; закладные под карниз — до обшивки

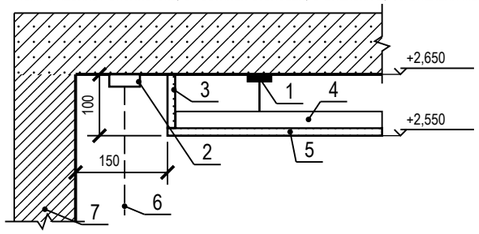

1 — анкер-клин к плите — по одному на подвес; подвес прямой, шаг 1000 мм

2 — карниз (шина), высота с верхом портьеры 80 мм

3 — стенка ниши — ГКЛ 12,5

4 — ПП 60×27 — каркас короба, основные через 1200 мм; соединители одноуровневые, шурупы LN 3,5×9


5 — низ короба нижнего уровня — ГКЛ 12,5; шурупы TN 3,5×25 через 170 мм

6 — портьера

7 — стена с окном

Сечение 1.2. Примыкание потолка к стене (М 1:10)

Пом. 1 Кабинет-библиотека, 3 Гостиная-столовая, 8 Спальня 2, 10 Спальня мастер; примыкание — теневой шов

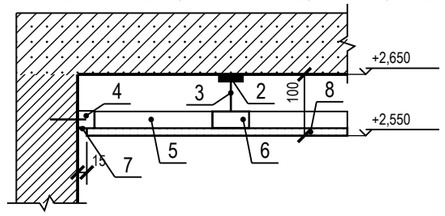

1 — плита перекрытия

2 — анкер-клин к плите — по одному на подвес

3 — подвес прямой, шаг 1000 мм

4 — ПН 28×27 по периметру — дюбель-гвоздь через ≤ 500 мм, не менее 3 на профиль

5 — ПП 60×27 несущий (вид) через 500 мм, в ПН

6 — ПП 60×27 основной (сечение) через 1200 мм; соединители одноуровневые, шурупы LN 3,5×9

7 — теневой профиль: шов 15 мм, зазор 3 мм; стена под шов выровнена

8 — ГКЛ 12,5 по П113; шурупы TN 3,5×25 через 170 мм

Допущения и предложения на листе

Основа листа: размеры сняты со скана обмерного плана KV design (см): часть подписей не читается, помещения выровнены по читаемым размерам; контрольный обмер не выполнен (К-1); высота потолка 2650 мм принята по отметкам обмера (Н = 2,50…2,66 м, ригель 2,28 м) — уточнить при обмере (К-2); толщины стен 300 / 120 мм приняты, межквартирная стена и колонны — по скану, не замерены (К-1); разрешённая мощность 15 кВт принята по типовым ТУ; при объединении двух квартир — переоформление ТУ (К-4); подрайон климата не задан — принят не северный (жилые от 2,5 м) (К-8).

См. лист открытых вопросов (лист 6, записи К-1, К-2, К-4, К-8).

Примечания

1. Сечения потолков М 1:10 по помещениям с нишами LED и нишами под шторы: отметки и размеры этого помещения от ±0,000 чистого пола (м, мм). Положение — по плану потолков (лист 45): короб и ниша LED — по линиям ленты, ниша под шторы — у стены с окном; типовые узлы по группам помещений — на листе 46.
2. Крепёж: подвес прямой к плите на анкер-клине — по одному на подвес (Knauf П113); ПН к стенам — дюбель-гвоздь через ≤ 500 мм, не менее 3 на профиль (серия 1.045.9-2.08); лист 12,5 — шурупы TN 3,5×25 через 170 мм (СП 163, табл. 15); профили между собой — соединители одноуровневые, шурупы LN 3,5×9.
3. Изделие карниза, профиля LED и галтели подписано артикулом из данных; где артикул не выбран, сечение дано по габаритам из данных (ширина и глубина ниши, щель под свет), изделие подбирается по ним.

1000 мм · печать 1:1

Изм.	Кол.уч	Лист	№ док.	Подп.	Дата
Разраб.		Кырлан А.С.			04.11.26
Пров.					
ГИП					
Н. контр.					
Утв.					

ГД-2026-009-АИ

Квартира 103 м²

Общая площадь 100,72* м² · * размеры со скана, не замерены (реестр — л. 6, 7, К-1)

Дизайн-проект интерьера

Стадия	Лист	Листов
РП	48	120

Сечения потолков М 1:10

М 1:10

Кырлан Александр Сергеевич


выпуск 04.11.2026 № 20cec94f32 · стр. 54 из 130

Раскладка плитки. Планы полов


Раскладка от чистовых размеров · размеры в мм · отметки от ±0,000

ПРЕДВАРИТЕЛЬНО · не для производства работ · открыто пунктов: 8 (реестр — л. 6, 7)

Фрагмент 1. Ванная (пом. 6). Пол 600×600, шов 2 мм, М 1:25

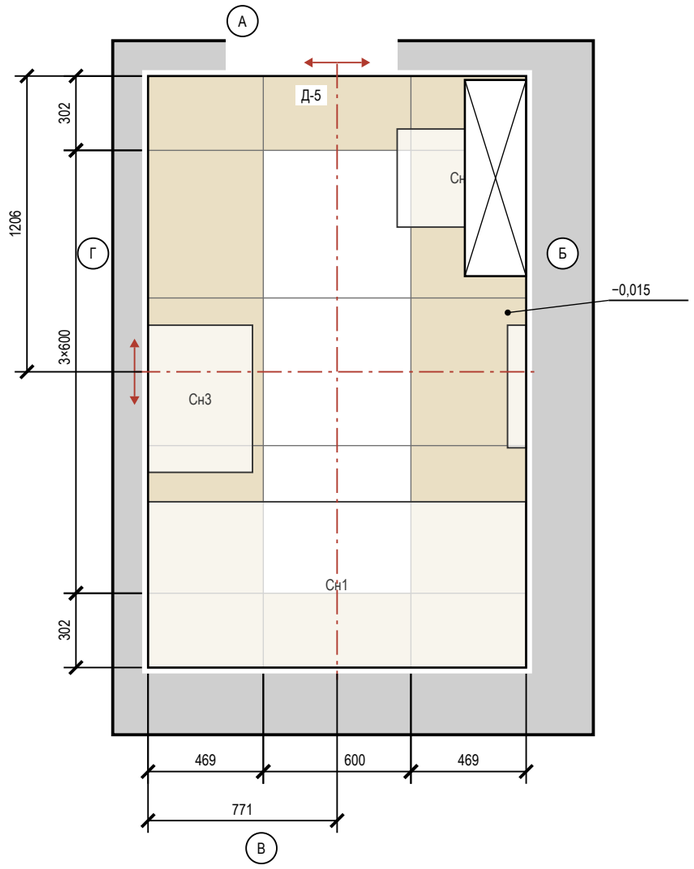

Фрагмент 2. Ванная мастер (пом. 11). Пол 600×600, шов 2 мм, М 1:25

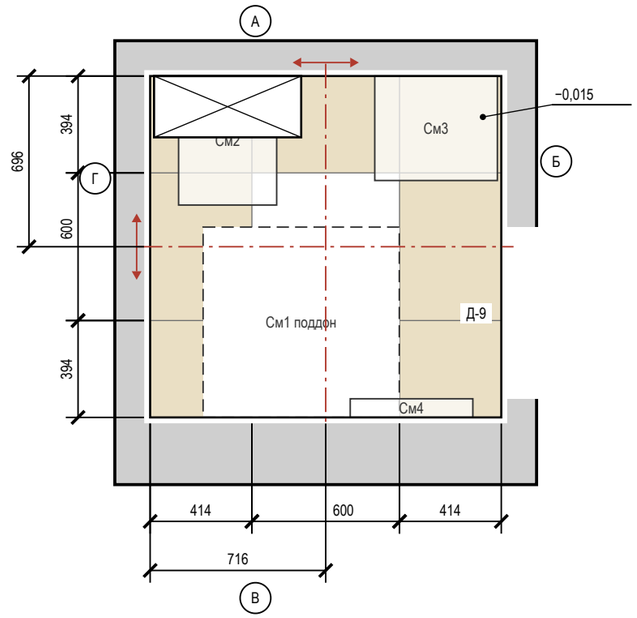

Ведомость материалов

Материал	Класс, код	Норма расхода	Кол-во
Затирка	CG2WA Mapei Ultracolor Plus 132	(a+b)/ab·шов·t·1,6	3,0 кг
Затирка	CG2WA	(a+b)/ab·шов·t·1,6	1,0 кг
Клей	C2 TE S1 Ceresit CM 17	1,5 кг/м²·мм, слой 5	297 кг (12 меш.)
Клей	C2 TE S1	1,5 кг/м²·мм, слой 5	105 кг (5 меш.)
Гидроизоляция	обмазочная, 2 слоя: пол, стены по периметру и зоны замачивания	по ТУ	18,7 м²
Демпф. лента	по периметру пола из плитки		27,1 м

Допущения и предложения на листе

Основа листа: размеры сняты со скана обмерного плана KV design (см): часть подписей не читается, помещения выровнены по читаемым размерам; контрольный обмер не выполнен (К-1); высота потолка 2650 мм принята по отметкам обмера (Н = 2,50…2,66 м, ригель 2,28 м) — уточнить при обмере (К-2); толщины стен 300 / 120 мм приняты, межквартирная стена и колонны — по скану, не замерены (К-1); разрешённая мощность 15 кВт принята по типовым ТУ; при объединении двух квартир — переоформление ТУ (К-4); подрайон климата не задан — принят не северный (жилые от 2,5 м) (К-8).

Знак «**» — предложение проектировщика, заказчиком не утверждено (согласовать с заказчиком): пол пом. 6, 11 — пирог пола: стяжка 33 мм и обмазочная гидроизоляция добавлены разработчиком проекта; артикул изделия не выбран: позиция описана характеристиками («аналог по характеристикам»), артикул выбирается при закупке.

См. лист открытых вопросов (лист 6, записи К-1, К-2, К-4, К-8).

Ведомость плитки

Помещение, поверхность	Плитка, код	Формат	Шов	S, м²	Целых	Подр.	С запасом
Ванная, пол	Atlas Concorde Marvel Travertine Sand Cross 60×60 Matte Sensitech, арт. AFUL (той же коллекции, что стены A8UZ; тон сверить по образцу)	600×600	2	3,91	3	12	17
Ванная, стены А–Г	A8UZ	600×1200	2	17,04	13	19	36
Ванная, короб инсталляции	A8UZ	600×1200	2	1,76	0	6	7
Ванная мастер, пол	Atlas Concorde Marvel Travertine Sand Cross 60×60 Matte Sensitech, арт. AFUL (той же коллекции, что стены A8UZ; тон сверить по образцу)	600×600	2	2,13	0	8	9
Ванная мастер, стены А–Г	A8UZ	600×1200	2	11,85	5	19	28
Ванная мастер, короб инсталляции	A8UZ	600×1200	2	1,47	1	3	5
Прихожая-холл, пол	A8UZ	600×1200	2	12,91	0	20	22
Итого 600×600				6,04	3	20	26
Итого 600×1200				**45,03**	**19**	**67**	**98**

Условные обозначения

- плитка целая; тонкая линия — шов
- плитка с подрезкой (размер — на цепочке)
- ось старта; стрелки — направление укладки
- сантехприбор: габарит, высота по практике
- поддон душа — плитку пола под ним не кладут
- короб инсталляции: плитка пола — до короба
- отметка чистого пола на полке выноски, м
- (А) обозначение стены А–Г (как на развёртках)

Примечания

1. Раскладка от чистовых размеров: стены санузлов теряют 10 + 5 + 9 = 24 мм на сторону (штукатурка, клей, плитка); подрезки — чистые, без шва.
2. Старт — от центра помещения (штрихпунктир, стрелки — направление укладки); размер старта — от чистовых стен Г и А.
3. Раскладка пола «Прихожая-холл» — на листе «Раскладка плитки. Прихожая-холл».
4. Калибр партии не задан — до укладки замерить (рабочий размер W, ГОСТ 13996-2019) и пересчитать подрезки.
5. Количество: целые по раскладке + по одной на подрезку, запас 10 %; один артикул — одна партия и тон. Исключены поддон, короб, проёмы и места за коробом; S — по чистым граням: стены нетто = зона облицовки по ведомости отделки − место за коробом инсталляции 1,68 м² (плитку за коробом не кладут), короб — отдельной строкой.
6. Клей C2 TE S1 Ceresit CM 17; C2 TE S1 (ГОСТ Р 56387-2018), затирка CG2WA Mapei Ultracolor Plus 132; CG2WA; расход — по ТУ выбранной марки.
7. Гидроизоляция: пол и стены 200 мм от ЧП; над ванной — до 2000 и 300 мм за борт (пом. 6), у душа — до 2000 и 500 мм за поддон (пом. 11) (см. развёртки); акт скрытых работ, пролив 24 ч.
8. Швы пола совмещены со швами стены А; по периметру — демпферная лента.
9. Отметка чистого пола −0,015, порог 15 мм; стык с соседним покрытием — по оси полотна двери.

1000 мм · печать 1:1

Изм.	Кол.уч	Лист	№ док.	Подп.	Дата
Разраб.		Кырлан А.С.			04.11.26
Пров.					
ГИП					
Н. контр.					
Утв.					

ГД-2026-009-АИ

Квартира 103 м²

Общая площадь 100,72* м² · * размеры со скана, не замерены (реестр — л. 6, 7, К-1)

Дизайн-проект интерьера

Стадия	Лист	Листов
РП	49	120

Раскладка плитки. Планы полов

М 1:25


Кырлан Александр Сергеевич

Раскладка плитки. Прихожая-холл

Раскладка от чистовых размеров · размеры в мм · высоты фартука от чистого пола

ПРЕДВАРИТЕЛЬНО · не для производства работ · открыто пунктов: 8 (реестр — л. 6, 7)

Фрагмент 1. Прихожая-холл (пом. 4). Пол 600×1200, шов 2 мм, М 1:20

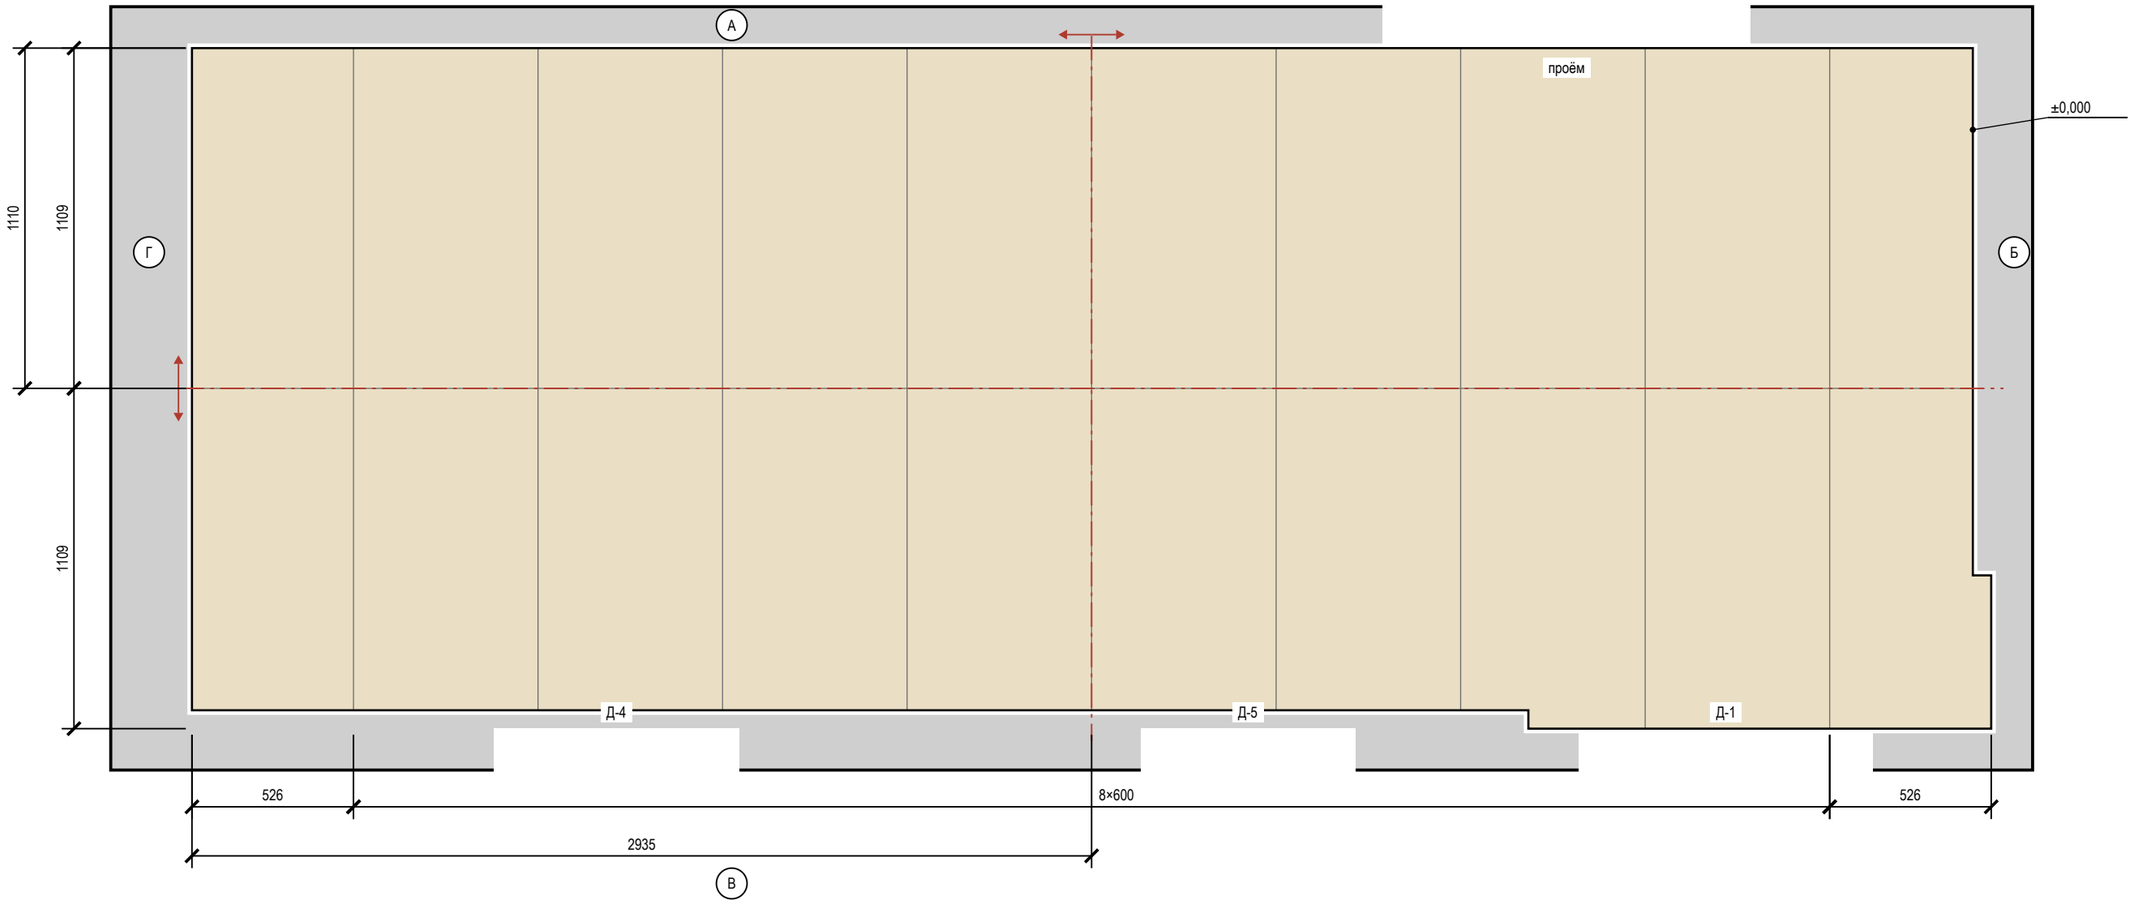

Условные обозначения

- плитка целая; тонкая линия — шов
- плитка с подрезкой (размер — на цепочке)
- ось старта; стрелки — направление укладки
- отметка чистого пола на полке выноски, м
- (А) обозначение стены А–Г (как на развёртках)

Подсчёт плитки

Поверхность	Формат	S, м²	Целых	Подр.	С запасом
Прихожая-холл, пол	600×1200	12,91	0	20	22

Примечания

1. Прихожая-холл: керамогранит 600×1200, длинная сторона — вдоль стен Б и Г, шов 2 мм, прямая раскладка от центра. Стены окрашены: раскладка от чистового контура минус штукатурка и шпаклёвка 15 мм на сторону (принято); подрезки 526 / 1109 мм, срез — под плинтус.
2. Прихожая-холл: деформационный зазор по периметру 8–10 мм под плинтусом; в проёмах — стык с соседним покрытием по оси полотна двери. Клей C2 TE S1, затирка CG2WA.
3. Клей, затирка и итог по форматам — в ведомостях листа «Раскладка плитки. Планы полов».

Допущения и предложения на листе

Основа листа: размеры сняты со скана обмерного плана KV design (см): часть подписей не читается, помещения выровнены по читаемым размерам; контрольный обмер не выполнен (К-1); высота потолка 2650 мм принята по отметкам обмера (Н = 2,50…2,66 м, ригель 2,28 м) — уточнить при обмере (К-2); толщины стен 300 / 120 мм приняты, межквартирная стена и колонны — по скану, не замерены (К-1); разрешённая мощность 15 кВт принята по типовым ТУ; при объединении двух квартир — переоформление ТУ (К-4); подрайон климата не задан — принят не северный (жилые от 2,5 м) (К-8).

Знак «**» — предложение проектировщика, заказчиком не утверждено (согласовать с заказчиком): плинтус пом. 4 — артикул изделия не выбран: позиция описана характеристиками («аналог по характеристикам»), артикул выбирается при закупке.

См. лист открытых вопросов (лист 6, записи К-1, К-2, К-4, К-8).

1000 мм · печать 1:1

Изм.	Кол.уч	Лист	№ док.	Подп.	Дата
Разраб.		Кырлан А.С.			04.11.26
Пров.					
ГИП					
Н. контр.					
Утв.					

ГД-2026-009-АИ

Квартира 103 м²

Общая площадь 100,72* м² · * размеры со скана, не замерены (реестр — л. 6, 7, К-1)

Дизайн-проект интерьера

Стадия	Лист	Листов
РП	50	120

Раскладка плитки. Прихожая-холл


М 1:20

Кырлан Александр Сергеевич

Раскладка плитки. Ванная. Развёртки стен

ПРЕДВАРИТЕЛЬНО · не для производства работ · открыто пунктов: 8 (реестр — л. 6, 7)

Пом. 6 · вид изнутри помещения · размеры в мм · высоты от чистого пола, отметки от ±0,000

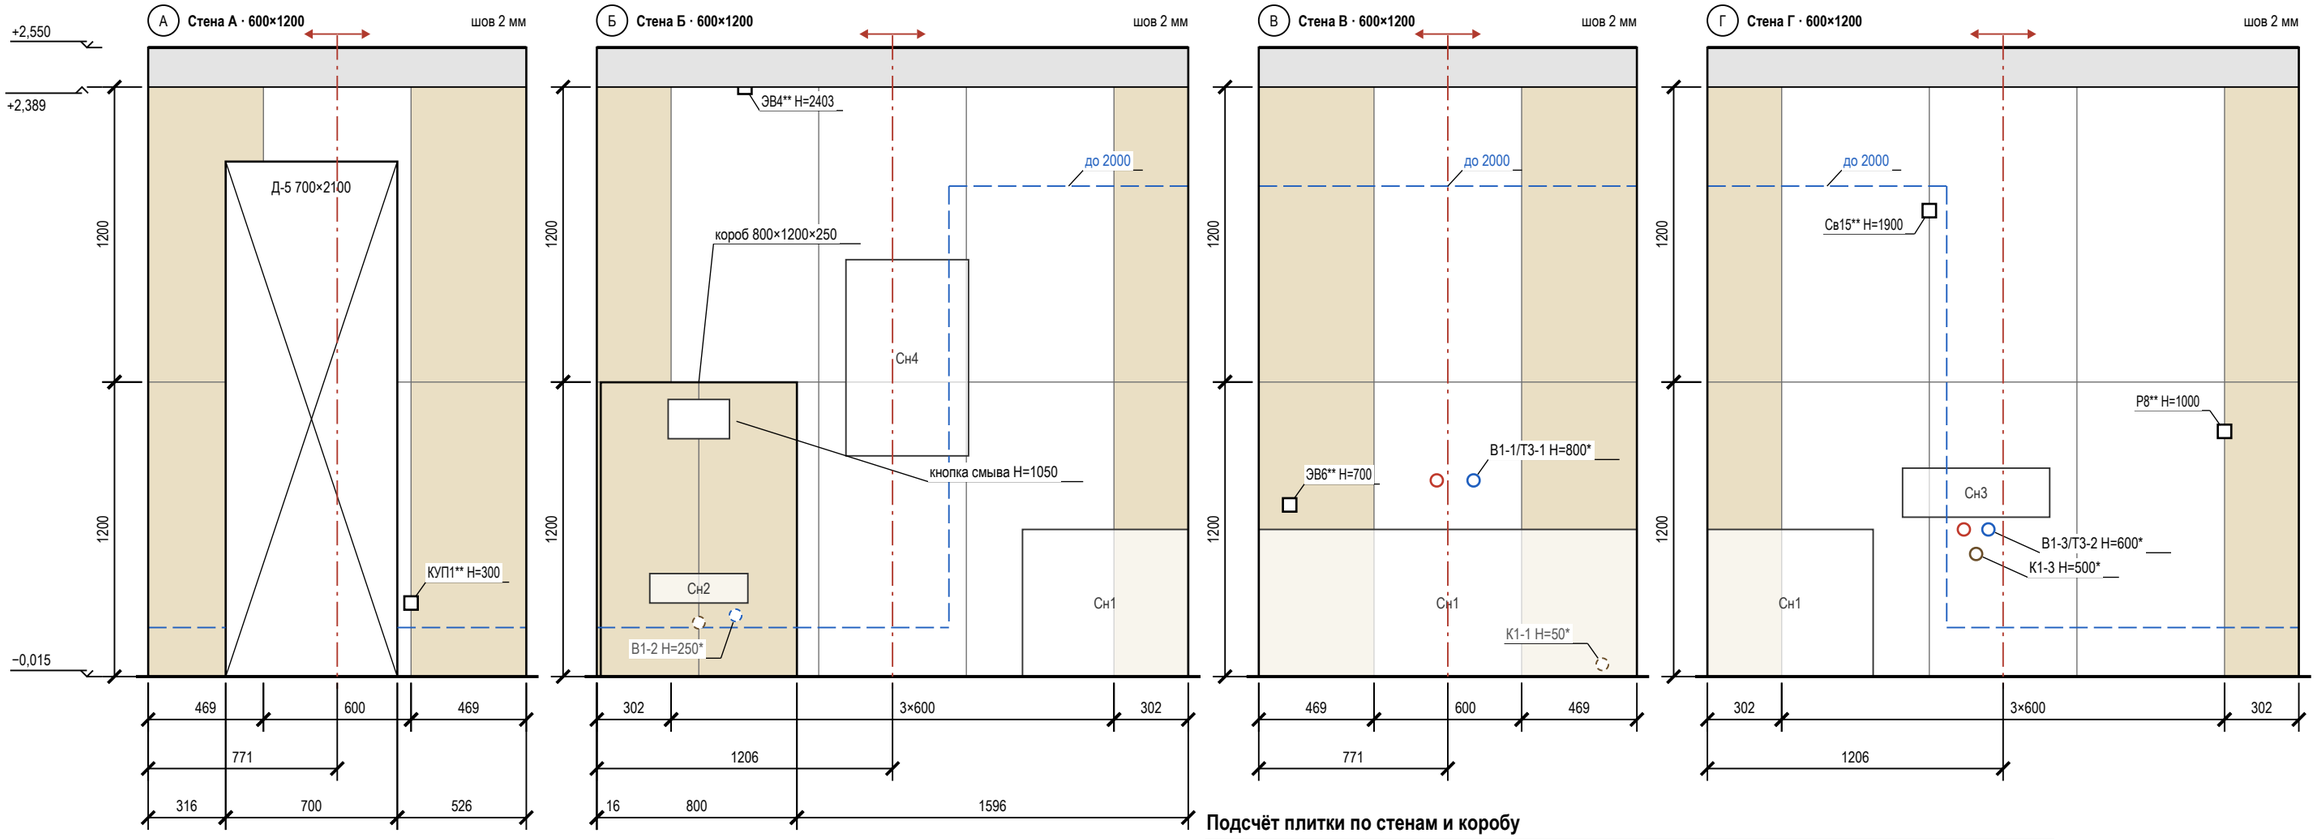

Подсчёт плитки по стенам и коробу

Поверхность	L × H, мм	S, м²	Целых	Подр.	С запасом	Подрезки: край / верх, мм
стена А	1542 × 2404	2,35	0	6	7	469 / 469; целый ряд
стена Б	2412 × 2404	4,95	5	5	11	302 / 302; целый ряд
короб (ст. Б)	800×1200×250	1,76	0	6	7	лицо 399 / 399; бок. 250
стена В	1542 × 2404	3,82	2	4	7	469 / 469; целый ряд
стена Г	2412 × 2404	5,91	6	4	11	302 / 302; целый ряд
Итого		**18,80**	**13**	**25**	**43**	

Сдвиг точек под раскладку

Точка (ВК, ЭОМ)	Стена	Проект: от угла / H	Под раскладку: от угла / H	Сдвиг, мм
ЭВ6**	В	126 / 700	169 / 700	+43 в центр плитки

Условные обозначения

- плитка целая; тонкая линия — шов
- плитка с подрезкой (размер — на цепочке)
- ось старта; стрелки — направление укладки
- верх гидроизоляции: 200 от ЧП, в мокрой зоне — «до …»
- проём — не облицовывается
- сантехприбор: габарит, высота по практике
- короб инсталляции, в нём кнопка смыва 250×160
- вывод В1 (код — в ведомости привязок)
- вывод Т3 (код — в ведомости привязок)
- вывод К1 (код — в ведомости привязок)
- вывод за прибором / в коробе (не на сетке)
- электроточка: марка и H — по листам ЭОМ
- отметка уровня, м: ±0,000 — чистый пол жилых помещений
- низ потолка; серая полоса — стена без плитки
- А — обозначение стены А–Г (как на развёртках)

1000 мм · печать 1:1

Примечания

1. Вид изнутри, стены по часовой стрелке А → Г. Высоты — от чистого пола (−0,015), отметки — от ±0,000. Раскладка от чистовых размеров (штукатурка 10 + клей 5 + плитка 9 мм), подрезки чистые; старт — от оси стены, ряды от пола целыми.
2. Верх плитки +2,389, потолок +2,550, зазор 161 мм: потолок ГКЛ опустить до +2,392 (шов 3 мм, герметик) — согласовать с монтажником ГКЛ; иначе профиль-окантовка, полосу окрасить в цвет потолка. Подрезной ряд 156 мм не делать.
3. Точки из таблицы сдвигов переносятся до черновой разводки (ЭОМ — по тем же числам).
4. Выводы ВК стоят по оси прибора и с прибором не двигаются — привязки по «Плану выводов сантехники» без сдвига; вне сетки (В1-1/Т3-1, В1-3/Т3-2, К1-3) отверстие в плитке коронкой по той же привязке, плитку не сдвигать.
5. Выводы — по «Плану выводов сантехники», электроточки — по ЭОМ, «*» — высота по практике; за приборами и в коробе (В1-2, К1-2, К1-1) — штриховым кольцом.
6. Гидроизоляция: 200 мм от ЧП по периметру; над ванной — до 2000 и 300 мм за борт (СП 29.13330.2011, п. 7.2 — на высоту замачивания); углы — лентой; акт скрытых работ, пролив.
7. Короб 800×1200×250: лицо 399 / 399 мм от оси кнопки смыва, боковины, полка; углы — запил 45° или профиль; за коробом плитку не кладут.
8. Между коробом и углом полоса 16 мм — довести короб до угла.

Допущения и предложения на листе. Основа листа: размеры сняты со скана обмерного плана KV design (см): часть подписей не читается, помещения выровнены по читаемым размерам; контрольный обмер не выполнен (К-1); высота потолка 2650 мм принята по отметкам обмера (H = 2,50…2,66 м, ригель 2,28 м) — уточнить при обмере (К-2); толщины стен 300 / 120 мм приняты, межквартирная стена и колонны — по скану, не замерены (К-1); разрешённая мощность 15 кВт принята по типовым ТУ; при объединении двух квартир — переоформление ТУ (К-4); подрайон климата не задан — принят не северный (жилые от 2,5 м) (К-8). Знак «**» — предложено, не утверждено (согласовать): пол пом. 6, Св15, КУП1; ИЗ-1: Р8, ЭВ4, ЭВ6. См. лист открытых вопросов (лист 6, записи ИЗ-1, К-1, К-2, К-4, К-8).

Изм.	Кол.уч	Лист	№ док.	Подп.	Дата
Разраб.		Кырлан А.С.			04.11.26
Пров.					
ГИП					
Н. контр.					
Утв.					

ГД-2026-009-АИ

Квартира 103 м²

Общая площадь 100,72* м² · * размеры со скана, не замерены (реестр — л. 6, 7, К-1)

Дизайн-проект интерьера

Стадия	Лист	Листов
РП	51	120

Раскладка плитки. Ванная. Развёртки стен

М 1:25


Кырлан Александр Сергеевич

выпуск 04.11.2026 № 20cec94f32 · стр. 57 из 130

Раскладка плитки. Ванная мастер. Развёртки стен

ПРЕДВАРИТЕЛЬНО · не для производства работ · открыто пунктов: 8 (реестр — л. 6, 7)

Пом. 11 · вид изнутри помещения · размеры в мм · высоты от чистого пола, отметки от ±0,000

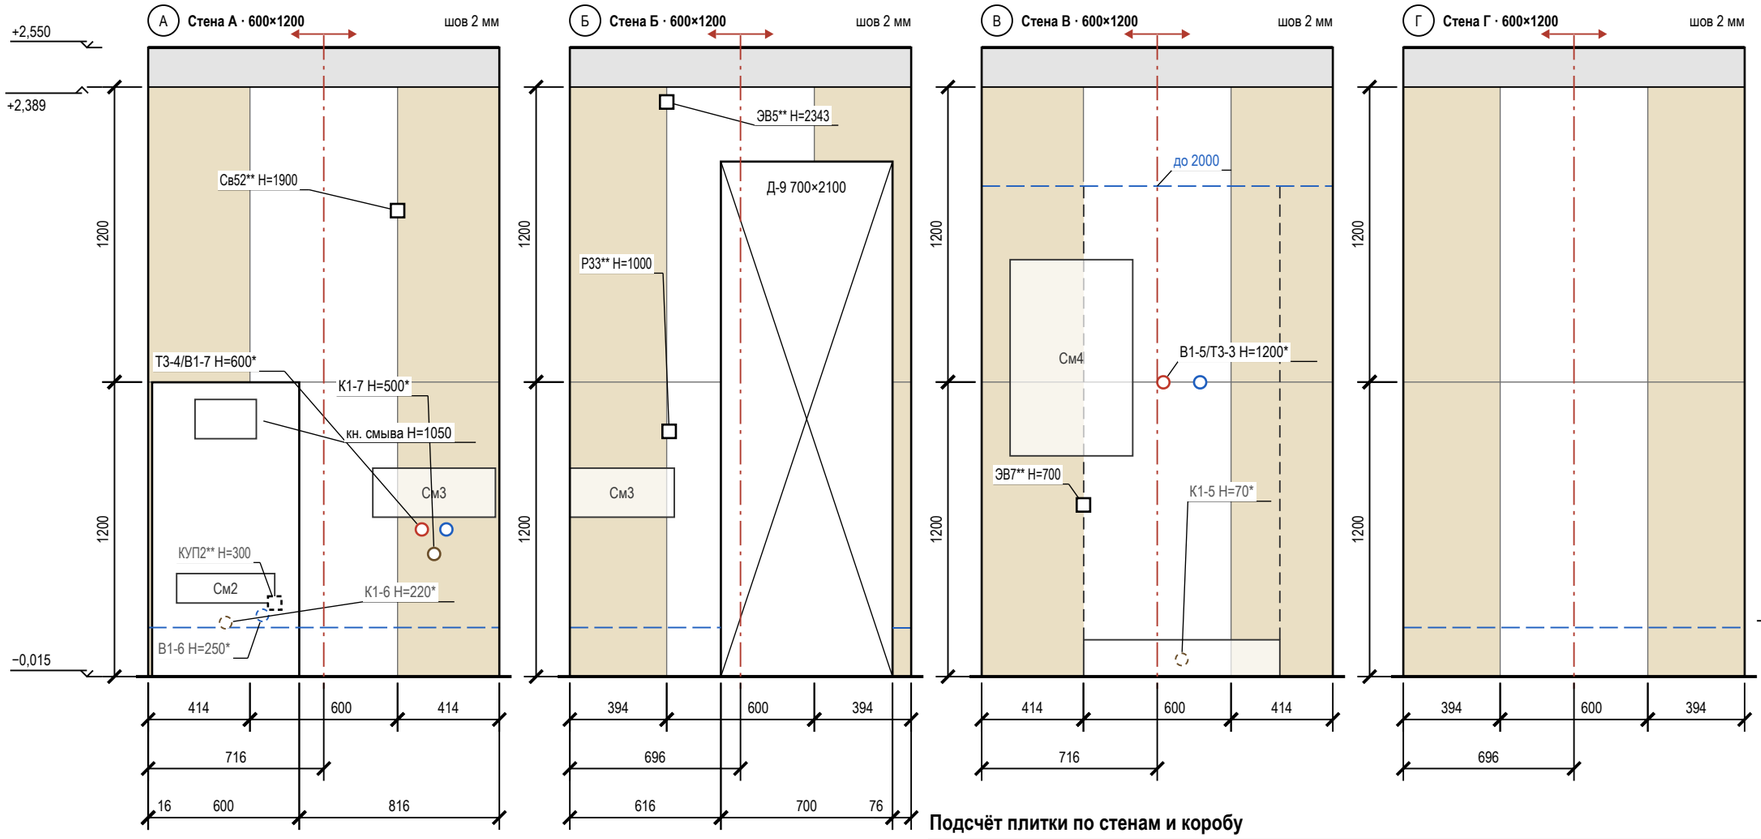

Условные обозначения

- плитка целая; тонкая линия — шов
- плитка с подрезкой (размер — на цепочке)
- ось старта; стрелки — направление укладки
- верх гидроизоляции: 200 от ЧП, в мокрой зоне — «до …»
- проём — не облицовывается
- сантехприбор: габарит, высота по практике
- граница душевой зоны (ограждение)
- короб инсталляции, в нём кнопка смыва 250×160
- вывод В1 (код — в ведомости привязок)
- вывод Т3 (код — в ведомости привязок)
- вывод К1 (код — в ведомости привязок)
- вывод за прибором / в коробе (не на сетке)
- электроточка: марка и Н — по листам ЭОМ
- отметка уровня, м: ±0,000 — чистый пол жилых помещений
- низ потолка; серая полоса — стена без плитки
- (А) обозначение стены А–Г (как на развёртках)

Подсчёт плитки по стенам и коробу

Поверхность	L × H, мм	S, м²	Целых	Подр.	С запасом	Подрезки: край / верх, мм
стена А	1432 × 2404	2,84	1	5	7	414 / 414; целый ряд
короб (ст. А)	600×1200×250	1,47	1	3	5	лицо 600; бок. 250
стена Б	1392 × 2404	1,99	0	6	7	394 / 394; целый ряд
стена В	1432 × 2404	3,56	2	4	7	414 / 414; целый ряд
стена Г	1392 × 2404	3,46	2	4	7	394 / 394; целый ряд
Итого		**13,32**	**6**	**22**	**33**	

Примечания

1. Вид изнутри, стены по часовой стрелке А → Г. Высоты — от чистого пола (−0,015), отметки — от ±0,000. Раскладка от чистовых размеров (штукатурка 10 + клей 5 + плитка 9 мм), подрезки чистые; старт — от оси стены, ряды от пола целыми.
2. Верх плитки +2,389, потолок +2,550, зазор 161 мм: потолок ГКЛ опустить до +2,392 (шов 3 мм, герметик) — согласовать с монтажником ГКЛ; иначе профиль-окантовка, полосу окрасить в цвет потолка. Подрезной ряд 156 мм не делать.
3. Открытые выводы и электроточки — на шве или в центре плитки (допуск 10 мм; плитка от 900 мм по высоте — на шве или не ближе 60 мм к нему).
4. Выводы ВК стоят по оси прибора и с прибором не двигаются — привязки по «Плану выводов сантехники» без сдвига; вне сетки (Т3-4/В1-7, К1-7, В1-5/Т3-3) отверстие в плитке коронкой по той же привязке, плитку не сдвигать.
5. Выводы — по «Плану выводов сантехники», электроточки — по ЭОМ, «*» — высота по практике; за приборами и в коробе (В1-6, К1-6, КУП2**, К1-5) — штриховым кольцом.
6. Гидроизоляция: 200 мм от ЧП по периметру; у душа — до 2000 и 500 мм за поддон (СП 29.13330.2011, п. 7.2 — на высоту замачивания); углы — лентой; акт скрытых работ, пролив.
7. Короб 600×1200×250: лицо 600 мм от оси кнопки смыва, боковины, полка; углы — запил 45° или профиль; за коробом плитку не кладут.
8. Между коробом и углом полоса 16 мм — довести короб до угла.
9. Линии узора (швы плитки, складки штор, рёбра радиаторов) прерываются у знаков и выносок — просвет между линиями не менее 0,7 мм.

Допущения и предложения на листе. Основа листа: размеры сняты со скана обмерного плана KV design (см): часть подписей не читается, помещения выровнены по читаемым размерам; контрольный обмер не выполнен (К-1); высота потолка 2650 мм принята по отметкам обмера (Н = 2,50…2,66 м, ригель 2,28 м) — уточнить при обмере (К-2); толщины стен 300 / 120 мм приняты, межквартирная стена и колонны — по скану, не замерены (К-1); разрешённая мощность 15 кВт принята по типовым ТУ; при объединении двух квартир — переоформление ТУ (К-4); подрайон климата не задан — принят не северный (жилые от 2,5 м) (К-8). Знак «**» — предложено, не утверждено (согласовать): пол пом. 11, Св52, ЭВ5, КУП2; ИЗ-1: Р33, ЭВ7. См. лист открытых вопросов (лист 6, записи ИЗ-1, К-1, К-2, К-4, К-8).

1000 мм · печать 1:1

Изм.	Кол.уч	Лист	№ док.	Подп.	Дата
Разраб.		Кырлан А.С.			04.11.26
Пров.					
ГИП					
Н. контр.					
Утв.					

ГД-2026-009-АИ

Квартира 103 м²

Общая площадь 100,72* м² · * размеры со скана, не замерены (реестр — л. 6, 7, К-1)

Дизайн-проект интерьера

Стадия	Лист	Листов
РП	52	120

Раскладка плитки. Ванная мастер. Развёртки стен

М 1:25

Кырлан Александр Сергеевич

выпуск 04.11.2026 № 20cec94f32 · стр. 58 из 130

07

Полы и отделка

Кырлан Александр Сергеевич

выпуск 04.11.2026 № 20cec94f32 · стр. 59 из 130


План полов

Покрытия, направление укладки, отметки чистого пола, стыки · размеры в мм · отметки в м

ПРЕДВАРИТЕЛЬНО · не для производства работ · открыто пунктов: 8 (реестр — л. 6, 7)

Условные обозначения

- тип 1 — инженерная доска, линии — вдоль доски
- тип 2 — инженерная доска, линии — вдоль доски
- тип 3 — керамогранит 600×1200, сетка — формат плитки
- тип 4 — инженерная доска, линии — вдоль доски
- тип 5 — керамогранит 600×600, сетка — формат плитки
- 1 — номер типа пола (экспликация полов)
- схема пола, без масштаба: плита — штриховка, стяжка — точки, звукоизоляция — зигзаг, гидроизоляция — утолщённая линия с заведением на стену
- направление укладки (длинная сторона доски)
- отметка чистого пола, м
- стык в проёме: без порога (б/п)
- стык в проёме: решение не задано
- стык в проёме: порог
- CT1 — марка стыка (ведомость стыков)
- стояк: К1 — канализация, В1 ХВС, Т3 — ГВС
- 1 — номер помещения, площадь м²

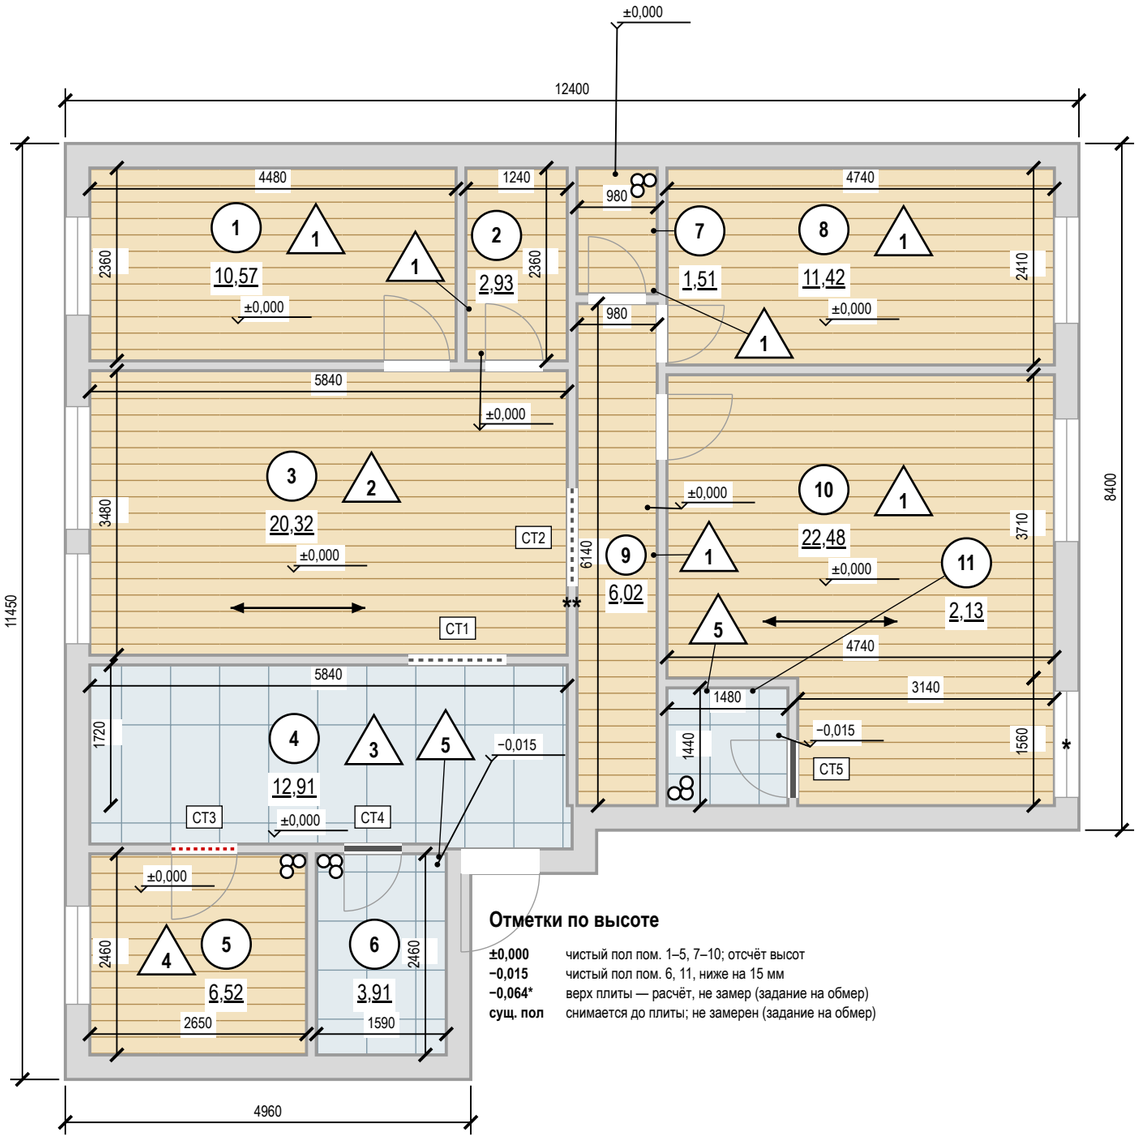

Отметки по высоте

±0,000	чистый пол пом. 1–5, 7–10; отсчёт высот
−0,015	чистый пол пом. 6, 11, ниже на 15 мм
−0,064*	верх плиты — расчёт, не замер (задание на обмер)
сущ. пол	снимается до плиты; не замерен (задание на обмер)

Экспликация полов

Номер помещения	Тип пола	Схема пола	Данные элементов пола (наименование, толщина, основание), мм	Площадь, м²
1, 2, 7, 8, 9, 10	1		Инженерная доска на клею — 14 Стяжка ЦПС М200 — 50 Плита перекрытия Всего 64 мм; ЧП ±0,000, верх плиты −0,064	54,93
3	2		Инженерная доска дуб на клею — 14 Клей паркетный МС-полимерный — 1 Стяжка ЦПС М300 (В22,5), фибра, по звукоизоляции — 49 Плита перекрытия монолитная Всего 64 мм; ЧП ±0,000, верх плиты −0,064	20,32
4	3		Керамогранит на клею С2 TE S1 — 14 Стяжка ЦПС М200 — 50 Плита перекрытия Всего 64 мм; ЧП ±0,000, верх плиты −0,064	12,91
5	4		Инженерная доска дуб на клею — 14 Клей паркетный МС-полимерный — 1 Гидроизоляция полиуретановая, 2 слоя (зона мойки и острова) — 2 Стяжка ЦПС М300 (В22,5), фибра, по звукоизоляции — 47 Плита перекрытия монолитная Всего 64 мм; ЧП ±0,000, верх плиты −0,064	6,52
6, 11	5		Керамогранит на клею С2 TE S1 — 14 Гидроизоляция обмазочная, 2 слоя, с заведением на стены 200 мм — 2 Стяжка ЦПС М200 — 33 Плита перекрытия Всего 49 мм; ЧП −0,015, верх плиты −0,064	6,04
			Итого	**100,72**

Стыки покрытий в проёмах

Марка	Проём	Типы пола	Отметки ЧП	Решение
CT1	3–4	2 / 3	±0,000 / ±0,000	б/п
CT2	3–9	2 / 1	±0,000 / ±0,000	б/п
CT3	5–4 (Д-4)	4 / 3	±0,000 / ±0,000	не задано
CT4	6–4 (Д-5)	5 / 3	−0,015 / ±0,000	порог h=15 мм
CT5	11–10 (Д-9)	5 / 1	−0,015 / ±0,000	порог h=15 мм

Допущения и предложения на листе. Знак «*» принято (замерить): Ст К1-3, Ст В1-3, Ст Т3-3. Знак «**» предложено (согласовать): плинтус пом. 1–5, 7–10, акцент пом. 3, фартук пом. 5, пол пом. 6, 11. См. лист открытых вопросов (лист 6).

Примечания

1. За отметку ±0,000 принят чистый пол, не существующий (блок отметок). Площади — по чистым размерам помещений, м²; размеры — в мм.
2. Стык разнотипных покрытий — по оси дверного полотна (под полотном в закрытом положении); решение стыка — по ведомости стыков.
3. Размеры помещений в свету (ширина × длина, мм), не поместившиеся на плане: пом. 4 — 5840 × 1720, 5900 × 470, 1540 × 60; пом. 7 — 980 × 1540.
4. Пол санузлов ниже смежных помещений на 15 мм за счёт меньшей толщины стяжки (верх плиты общий — по экспликации полов); гидроизоляция по стяжке с заведением на стены не менее 200 мм (СП 29.13330.2011, п. 7.2), до облицовки — тест проливом и акт скрытых работ.
5. Трубопроводы в конструкции пола не прокладываются: пирог пола 49–64 мм не вмещает выпуски канализации с уклоном — выпуски К1 ведутся по стенам над чистым полом в коробах (лист 34).
6. Звукоизоляционный слой под стяжкой проектом не предусмотрен (стяжка по плите): приведённый уровень ударного шума перекрытия с полом Lnw не более 60 дБ (СП 51.13330.2011, табл. 2) подтвердить по данным дома; при превышении — плавающая стяжка по звукоизоляции с демпферной лентой по контуру и у стояков, пирог пересчитать.
7. Штучные покрытия (инженерная доска): направление — по стрелке; влажность основания по СМ не более 2,0 % (по ТУ изготовителя).
8. Ровность основания — просвет под 2-метровой рейкой не более 2 мм: пом. 1, 2, 3, 5, 7, 8, 9, 10 (инженерная доска), пом. 4, 6, 11 (керамогранит); проверить до укладки покрытия (СП 71.13330.2017, табл. 8.5).
9. Сетка на плитке — условная, в размер формата; точка старта и раскладка — по листу раскладки плитки.
10. Узор покрытия (заливка-код типа пола) прерывается под надписями — площадями помещений и отметками чистого пола.
11. Пироги полов — по экспликации полов: слои сверху вниз, толщины в мм; гидроизоляция мокрых зон — в пироге и в ведомости отделки; схема пола — без масштаба.

1000 мм · печать 1:1

Изм.	Кол.уч	Лист	№ док.	Подп.	Дата
Разраб.		Кырлан А.С.			04.11.26
Пров.					
ГИП					
Н. контр.					
Утв.					

ГД-2026-009-АИ

Квартира 103 м²

Общая площадь 100,72* м² · * размеры со скана, не замерены (реестр — л. 6, 7, К-1)

Дизайн-проект интерьера

Стадия	Лист	Листов
РП	53	120

План полов

М 1:75

Кырлан Александр Сергеевич

выпуск 04.11.2026 № 20cec94f32 · стр. 60 из 130

Ведомость отделки помещений. Лист 1 из 3

Потолки, стены, низ стен, полы · площади в м², длины в м · отметки в м

Ведомость отделки помещений (форма 1 прил. А ГОСТ 21.501-2018). Лист 1 из 3

№	Наименование помещения	Потолок			Стены и перегородки			Низ стен (плинтус)			Пол		Примечание
		Вид отделки	Код цвета	S, м²	Вид отделки	Код цвета	S, м²	Вид отделки	Код цвета	L, м	Вид отделки	S, м²	
1	Кабинет-библиотека 10,57 м²	ГКЛ по каркасу П113, отм. +2,550; окраска, Tikkurila Anti-Reflex 2, глубокоматовая, 2 слоя, подготовка Q3	NCS S 0502-Y	10,57	Окраска, Farrow & Ball Modern Emulsion, матовая, 2 слоя, подготовка Q3 Акцент — стена А: окраска, Farrow & Ball Modern Emulsion, матовая, 2 слоя, подготовка Q3	Farrow & Ball No. 291 Farrow & Ball No. 289	19,91 11,42	Плинтус МДФ h=83 мм, Ultrawood Base 5340, ЛДФ под окраску, 83×15 мм, 2440 мм (арт. LDF-BASE-5340)	Farrow & Ball No. 291	12,9	Инженерная доска, 1167-4250, 2100×127 мм, на клею; тип 1, отм. ЧП ±0,000	10,57	Н стен 2550 (до потолка); плинтус в цвет: стены
2	Кладовая 2,93 м²	Существующий потолок, отм. +2,650; окраска, Tikkurila Anti-Reflex 2, глубокоматовая, 2 слоя, подготовка Q3	NCS S 0502-Y	2,93	Окраска, Tikkurila Harmony, матовая, 2 слоя, подготовка Q3	NCS S 0502-Y	17,61	Плинтус МДФ h=83 мм, Ultrawood Base 5340, ЛДФ под окраску, 83×15 мм, 2440 мм (арт. LDF-BASE-5340)	NCS S 0502-Y	6,5	Инженерная доска, 1167-4250, 2100×127 мм, на клею; тип 1, отм. ЧП ±0,000	2,93	Н стен 2650 (до потолка); плинтус в цвет: стены
3	Гостиная-столовая 20,32 м²	ГКЛ по каркасу П113, отм. +2,550; окраска, Farrow & Ball Modern Emulsion, матовая, 2 слоя, подготовка Q3	Farrow & Ball No. 291	20,32	Окраска, Farrow & Ball Modern Emulsion, матовая, 2 слоя, подготовка К3 Акцент — стена А: окраска, Farrow & Ball Modern Emulsion, матовая, 3 слоя, аналог: интерьерная краска Farrow & Ball Modern Emulsion в цвете веера No. 255, матовая, подготовка К3	Farrow & Ball No. 291 Farrow & Ball No. 255	23,57 11,74	Плинтус МДФ h=83 мм, Ultrawood Base 5340, ЛДФ под окраску, 83×15 мм, 2440 мм (арт. LDF-BASE-5340)	Farrow & Ball No. 291	14,7	Инженерная доска, 1167-4250, 2100×127 мм, на клею; тип 2, отм. ЧП ±0,000	20,32	Н стен 2550 (до потолка); класс мокрого истирания по EN 13300 и блеск линейки Farrow & Ball Modern Emulsion — по ТУ производителя, в базе не сверены; потолок в цвет стен (No. 291) — краска бренда веера, Farrow & Ball Modern Emulsion; класс мокрого истирания по EN 13300 и блеск линейки Farrow & Ball Modern Emulsion — по ТУ производителя, в базе не сверены; колеруется в код стен, но по эмали на МДФ: сличать отдельным выкрасом на своей подложке (выкрас № 10); плинтус в цвет: стены
4	Прихожая-холл 12,91 м²	ГКЛ по каркасу П113, отм. +2,550; окраска, Tikkurila Anti-Reflex 2, глубокоматовая, 2 слоя, подготовка Q3	NCS S 0502-Y	12,91	Окраска, Farrow & Ball Modern Emulsion, матовая, 2 слоя, подготовка Q3	Farrow & Ball No. 291	33,88	Плинтус МДФ h=83 мм, Ultrawood Base 5340, ЛДФ под окраску, 83×15 мм, 2440 мм (арт. LDF-BASE-5340)	Farrow & Ball No. 291	12,6	Керамогранит, A8UZ, 600×1200×9 мм; тип 3, отм. ЧП ±0,000	12,91	Н стен 2550 (до потолка); матовая моющаяся, класс 1 EN 13300 — осознанно вместо полуматовой; плинтус в цвет: стены

Примечания

1. Ведомость продолжена на листе 2 из 3; итоги, сводка площадей и примечания — на последнем листе ведомости.

Допущения и предложения на листе

Основа листа: размеры сняты со скана обмерного плана KV design (см): часть подписей не читается, помещения выровнены по читаемым размерам; контрольный обмер не выполнен (К-1); высота потолка 2650 мм принята по отметкам обмера (Н = 2,50…2,66 м, ригель 2,28 м) — уточнить при обмере (К-2); толщины стен 300 / 120 мм приняты, межквартирная стена и колонны — по скану, не замерены (К-1); разрешённая мощность 15 кВт принята по типовым ТУ; при объединении двух квартир — переоформление ТУ (К-4); подрайон климата не задан — принят не северный (жилые от 2,5 м) (К-8).

Знак «**» — предложение проектировщика, заказчиком не утверждено (согласовать с заказчиком): плинтус пом. 1–5, 7–10, акцент пом. 3, фартук пом. 5 — артикул изделия не выбран: позиция описана характеристиками («аналог по характеристикам»), артикул выбирается при закупке; пол пом. 6, 11 — пирог пола: стяжка 33 мм и обмазочная гидроизоляция добавлены разработчиком проекта; артикул изделия не выбран: позиция описана характеристиками («аналог по характеристикам»), артикул выбирается при закупке.

См. лист открытых вопросов (лист 6, записи К-1, К-2, К-4, К-8).

Изм.	Кол.уч	Лист	№ док.	Подп.	Дата
Разраб.		Кырлан А.С.			04.11.26
Пров.					
ГИП					
Н. контр.					
Утв.					

ГД-2026-009-АИ

Квартира 103 м²

Общая площадь 100,72* м² · * размеры со скана, не замерены (реестр — л. 6, 7, К-1)

Дизайн-проект интерьера	Стадия	Лист	Листов
	РП	54	120

Ведомость отделки помещений. Лист 1 из 3

М б/м

Кырлан Александр Сергеевич

выпуск 04.11.2026 № 20cec94f32 · стр. 61 из 130

Ведомость отделки помещений. Лист 2 из 3

Потолки, стены, низ стен, полы · площади в м², длины в м · отметки в м

Ведомость отделки помещений (форма 1 прил. А ГОСТ 21.501-2018). Лист 2 из 3

№	Наименование помещения	Потолок			Стены и перегородки			Низ стен (плинтус)			Пол		Примечание
		Вид отделки	Код цвета	S, м²	Вид отделки	Код цвета	S, м²	Вид отделки	Код цвета	L, м	Вид отделки	S, м²	
5	Кухня 6,52 м²	ГКЛВ по каркасу П113, отм. +2,550; окраска, Farrow & Ball Modern Emulsion, матовая, 2 слоя, подготовка Q3	Farrow & Ball No. 291	6,52	Окраска, Farrow & Ball Modern Emulsion, матовая, 2 слоя, подготовка К3 Фартук кухни (стена Б, В): облицовка керамогранитом, аналог: керамогранит матовый, тон F497, 600×600×9 мм, клей C2 TE S1, затирка CG2WA	Farrow & Ball No. 291 #F1F1EC	20,51 2,01	Плинтус МДФ h=83 мм, Ultrawood Base 5340, ЛДФ под окраску, 83×15 мм, 2440 мм (арт. LDF-BASE-5340)	Farrow & Ball No. 291	9,4	Инженерная доска, 1167-4250, 2100×127 мм, на клею; тип 4, отм. ЧП ±0,000	6,52	Н стен 2550 (до потолка); моющаяся матовая окраска Farrow & Ball Modern Emulsion (краска бренда веера No. 291,); класс мокрого истирания по EN 13300 и блеск линейки Farrow & Ball Modern Emulsion — по ТУ производителя, в базе не сверены; категория К3 по СП 71.13330.2017, табл. 7.5; по ГКЛ каркаса П113, моющаяся окраска Farrow & Ball Modern Emulsion; Q3 класс мокрого истирания по EN 13300 и блеск линейки Farrow & Ball Modern Emulsion — по ТУ производителя, в базе не сверены; колеруется в код стен, но по эмали на МДФ: сличать отдельным выкрасом на своей подложке (выкрас № 10); плинтус в цвет: стены
6	Ванная 3,91 м²	ГКЛВ по каркасу П113, отм. +2,550; окраска, Tikkurila Luja 7, матовая, 2 слоя, подготовка Q3	NCS S 0502-Y	3,91	Облицовка плиткой, A8UZ, 600×1200×9 мм, клей C2 TE S1, затирка CG2WA	Atlas Concorde A8UZ	18,00	нет			Керамогранит, Atlas Concorde Marvel Travertine Sand CrossMatte Sensitech, арт. AFUL (той же коллекции, что стены A8UZ; тон сверить по образцу), 600×600×9 мм; тип 5, отм. ЧП −0,015	3,91	Н стен 2565 (до потолка); гидроизоляция обмазочная, 2 слоя, с заведением на стены 200 мм; над ванной — до 2000 и 300 мм за борт (по пирогу пола); тест проливом и акт скрытых работ
7	Постирочная 1,51 м²	Существующий потолок, отм. +2,650; окраска, Tikkurila Anti-Reflex 2, глубокоматовая, 2 слоя, подготовка Q3	NCS S 0502-Y	1,51	Окраска, Tikkurila Harmony, матовая, 2 слоя, подготовка Q3	NCS S 0502-Y	11,89	Плинтус МДФ h=83 мм, Ultrawood Base 5340, ЛДФ под окраску, 83×15 мм, 2440 мм (арт. LDF-BASE-5340)	NCS S 0502-Y	4,3	Инженерная доска, 1167-4250, 2100×127 мм, на клею; тип 1, отм. ЧП ±0,000	1,51	Н стен 2650 (до потолка); плинтус в цвет: стены
8	Спальня 2 11,42 м²	ГКЛ по каркасу П113, отм. +2,550; окраска, Tikkurila Anti-Reflex 2, глубокоматовая, 2 слоя, подготовка Q3	NCS S 0502-Y	11,42	Окраска, Farrow & Ball Modern Emulsion, матовая, 2 слоя, подготовка Q3 Акцент — стена А: окраска, Farrow & Ball Modern Emulsion, матовая, 2 слоя, подготовка Q3	Farrow & Ball No. 291 Farrow & Ball No. 289	20,89 12,09	Плинтус МДФ h=83 мм, Ultrawood Base 5340, ЛДФ под окраску, 83×15 мм, 2440 мм (арт. LDF-BASE-5340)	Farrow & Ball No. 291	13,6	Инженерная доска, 1167-4250, 2100×127 мм, на клею; тип 1, отм. ЧП ±0,000	11,42	Н стен 2550 (до потолка); плинтус в цвет: стены
9	Коридор 6,02 м²	ГКЛ по каркасу П113, отм. +2,550; окраска, Tikkurila Anti-Reflex 2, глубокоматовая, 2 слоя, подготовка Q3	NCS S 0502-Y	6,02	Окраска, Farrow & Ball Modern Emulsion, матовая, 2 слоя, подготовка Q3	Farrow & Ball No. 291	29,17	Плинтус МДФ h=83 мм, Ultrawood Base 5340, ЛДФ под окраску, 83×15 мм, 2440 мм (арт. LDF-BASE-5340)	Farrow & Ball No. 291	10,8	Инженерная доска, 1167-4250, 2100×127 мм, на клею; тип 1, отм. ЧП ±0,000	6,02	Н стен 2550 (до потолка); матовая моющаяся, класс 1 EN 13300 — осознанно вместо полуматовой; плинтус в цвет: стены

Примечания

1. Ведомость продолжена на листе 3 из 3; итоги, сводка площадей и примечания — на последнем листе ведомости.

Допущения и предложения на листе

Основа листа: размеры сняты со скана обмерного плана KV design (см): часть подписей не читается, помещения выровнены по читаемым размерам; контрольный обмер не выполнен (К-1); высота потолка 2650 мм принята по отметкам обмера (Н = 2,50…2,66 м, ригель 2,28 м) — уточнить при обмере (К-2); толщины стен 300 / 120 мм приняты, межквартирная стена и колонны — по скану, не замерены (К-1); разрешённая мощность 15 кВт принята по типовым ТУ; при объединении двух квартир — переоформление ТУ (К-4); подрайон климата не задан — принят не северный (жилые от 2,5 м) (К-8).

Знак «**» — предложение проектировщика, заказчиком не утверждено (согласовать с заказчиком): плинтус пом. 1–5, 7–10, акцент пом. 3, фартук пом. 5 — артикул изделия не выбран: позиция описана характеристиками («аналог по характеристикам»), артикул выбирается при закупке; пол пом. 6, 11 — пирог пола: стяжка 33 мм и обмазочная гидроизоляция добавлены разработчиком проекта; артикул изделия не выбран: позиция описана характеристиками («аналог по характеристикам»), артикул выбирается при закупке.

См. лист открытых вопросов (лист 6, записи К-1, К-2, К-4, К-8).

Изм.	Кол.уч	Лист	№ док.	Подп.	Дата
Разраб.		Кырлан А.С.			04.11.26
Пров.					
ГИП					
Н. контр.					
Утв.					

ГД-2026-009-АИ

Квартира 103 м²

Общая площадь 100,72* м² · * размеры со скана, не замерены (реестр — л. 6, 7, К-1)

Дизайн-проект интерьера	Стадия	Лист	Листов
	РП	55	120

Ведомость отделки помещений. Лист 2 из 3

М б/м

Кырлан Александр Сергеевич

выпуск 04.11.2026 № 20cec94f32 · стр. 62 из 130

Ведомость отделки помещений. Лист 3 из 3

Потолки, стены, низ стен, полы · площади в м², длины в м · отметки в м

Ведомость отделки помещений (форма 1 прил. А ГОСТ 21.501-2018). Лист 3 из 3

№	Наименование помещения	Потолок			Стены и перегородки			Низ стен (плинтус)			Пол		Примечание
		Вид отделки	Код цвета	S, м²	Вид отделки	Код цвета	S, м²	Вид отделки	Код цвета	L, м	Вид отделки	S, м²	
10	Спальня мастер 22,48 м²	ГКЛ по каркасу П113, отм. +2,550; окраска, Tikkurila Anti-Reflex 2, глубокоматовая, 2 слоя, подготовка Q3	NCS S 0502-Y	22,48	Окраска, Farrow & Ball Modern Emulsion, матовая, 2 слоя, подготовка Q3 Акцент — стена А: окраска, Farrow & Ball Modern Emulsion, матовая, 2 слоя, подготовка Q3	Farrow & Ball No. 291 Farrow & Ball No. 289	31,48 12,09	Плинтус МДФ h=83 мм, Ultrawood Base 5340, ЛДФ под окраску, 83×15 мм, 2440 мм (арт. LDF-BASE-5340)	Farrow & Ball No. 291	18,5	Инженерная доска, 1167-4250, 2100×127 мм, на клею; тип 1, отм. ЧП ±0,000	22,48	Н стен 2550 (до потолка); плинтус в цвет: стены
11	Ванная мастер 2,13 м²	ГКЛВ по каркасу П113, отм. +2,550; окраска, Tikkurila Luja 7, матовая, 2 слоя, подготовка Q3	NCS S 0502-Y	2,13	Облицовка плиткой, A8UZ, 600×1200×9 мм, клей C2 TE S1, затирка CG2WA	Atlas Concorde A8UZ	12,57	нет			Керамогранит, Atlas Concorde Marvel Travertine Sand CrossMatte Sensitech, арт. AFUL (той же коллекции, что стены A8UZ; тон сверить по образцу), 600×600×9 мм; тип 5, отм. ЧП −0,015	2,13	Н стен 2565 (до потолка); гидроизоляция обмазочная, 2 слоя, с заведением на стены 200 мм; у душа — до 2000 и 500 мм за поддон (по пирогу пола); тест проливом и акт скрытых работ
	Итого			**100,72**			**288,83**			**103,5**		**100,72**	

Сводка площадей по материалам отделки

Поверхность	Материал / код цвета	Серия	Площадь, м²
Потолок	NCS S 0502-Y	Anti-Reflex 2	67,84
Потолок	Farrow & Ball No. 291	Modern Emulsion	26,84
Потолок	NCS S 0502-Y	Luja 7	6,04
Стены	Farrow & Ball No. 291	Modern Emulsion	179,41
Стены	Farrow & Ball No. 289	Modern Emulsion	35,60
Стены	NCS S 0502-Y	Harmony	29,50
Стены	Farrow & Ball No. 255	Modern Emulsion	11,74
Стены	облицовка плиткой 600×1200×9 мм, Atlas Concorde A8UZ	A8UZ	30,57
Фартук	облицовка керамогранитом, #F1F1EC	аналог: керамогранит матовый, тон F497	2,01

Допущения и предложения на листе

Основа листа: размеры сняты со скана обмерного плана KV design (см): часть подписей не читается, помещения выровнены по читаемым размерам; контрольный обмер не выполнен (К-1); высота потолка 2650 мм принята по отметкам обмера (Н = 2,50…2,66 м, ригель 2,28 м) — уточнить при обмере (К-2); толщины стен 300 / 120 мм приняты, межквартирная стена и колонны — по скану, не замерены (К-1); разрешённая мощность 15 кВт принята по типовым ТУ; при объединении двух квартир — переоформление ТУ (К-4); подрайон климата не задан — принят не северный (жилые от 2,5 м) (К-8).

Знак «**» — предложение проектировщика, заказчиком не утверждено (согласовать с заказчиком): плинтус пом. 1–5, 7–10, акцент пом. 3, фартук пом. 5 — артикул изделия не выбран: позиция описана характеристиками («аналог по характеристикам»), артикул выбирается при закупке; пол пом. 6, 11 — пирог пола: стяжка 33 мм и обмазочная гидроизоляция добавлены разработчиком проекта; артикул изделия не выбран: позиция описана характеристиками («аналог по характеристикам»), артикул выбирается при закупке.

См. лист открытых вопросов (лист 6, записи К-1, К-2, К-4, К-8).

Примечания

1. Площади поверхностей — по чистым граням стен до отделки: стены = периметр × высоту от чистого пола помещения до низа потолка минус проёмы (облицовка плиткой — до верха облицовки); плинтус = периметр минус дверные проёмы; пол и потолок — по площади помещения. Количество плиток по раскладке. Площади помещений — с учётом всех частей помещения; откосы в площадь стен не входят.
2. Акцентные стены и фартук — отдельными строками, их площадь вычтена из основной отделки стен помещения; фартук — над нижними модулями кухни от столешницы до низа навесных шкафов, где шкафов нет — на 600 мм.
3. Плинтус — длина по периметру за вычетом дверных проёмов; примыкания к наличникам и встроенной мебели — по развёрткам.
4. Формат плитки — Ш×В×Т (ширина × высота в положении укладки × толщина), мм; на полу — вдоль стен А/В × вдоль стен Б/Г.
5. Коды цвета — по веерам производителей; колеровка каждой краски одной партией, проверка выкраса при свете D65 и при лампах проекта.
6. Уровни подготовки Q1–Q4 — система Knauf, не норма ГОСТ/СП; допуски поверхностей — по СП 71.13330.2017 (действующая редакция).
7. «аналог:» — изделие задано характеристиками, марку и артикул согласовать с заказчиком до закупки.
8. Плавающая стяжка по звукоизоляции: демпферная (кромочная) лента по контуру помещения и у стояков (СП 51.13330.2011, п. 9.11); плинтус крепится только к стене.

Изм.	Кол.уч	Лист	№ док.	Подп.	Дата				
Разраб.		Кырлан А.С.			04.11.26	ГД-2026-009-АИ			
Пров.						Квартира 103 м² Общая площадь 100,72* м² · * размеры со скана, не замерены (реестр — л. 6, 7, К-1)			
ГИП						Дизайн-проект интерьера	Стадия	Лист	Листов
							РП	56	120
Н. контр.						Ведомость отделки помещений. Лист 3 из 3 М б/м	Кырлан Александр Сергеевич		
Утв.									

Колерная карта

Цвета и материалы по помещениям · палитра проекта · лист 1 из 2

Колерная карта по помещениям

Помещение	Поверхность	Образец	Поз.	Система и код цвета	Производитель, линейка / материал, артикул	Блеск	Класс истирания	LRV	Площадь
1. Кабинет-библиотека 10,57 м²	стены		**K1**	Farrow & Ball No. 291	Farrow & Ball · Modern Emulsion	матовая	1	73	19,9 м²
	акцент А		**K2**	Farrow & Ball No. 289	Farrow & Ball · Modern Emulsion	матовая	1	13	11,4 м²
	потолок		**K3**	NCS S 0502-Y	Tikkurila · Anti-Reflex 2	глубокомат.	2	95	10,6 м²
	пол		**KM1**	по образцу	Coswick · Вековые традиции · арт. 1167-4250				10,6 м²
	плинтус		**K4**	Farrow & Ball No. 291	МДФ · в цвет Farrow & Ball			73	12,9 м
2. Кладовая 2,93 м²	стены		**K5**	NCS S 0502-Y	Tikkurila · Harmony	матовая	1	95	17,6 м²
	потолок		**K3**	NCS S 0502-Y	Tikkurila · Anti-Reflex 2	глубокомат.	2	95	2,9 м²
	пол		**KM1**	по образцу	Coswick · Вековые традиции · арт. 1167-4250				2,9 м²
	плинтус		**K6**	NCS S 0502-Y	МДФ · в цвет NCS			95	6,5 м
3. Гостиная-столовая 20,32 м²	стены		**K1**	Farrow & Ball No. 291	Farrow & Ball · Modern Emulsion	матовая	1	73	23,6 м²
	акцент А		**K7**	Farrow & Ball No. 255	Farrow & Ball · Modern Emulsion	матовая	1	7	11,7 м²
	потолок		**K1**	Farrow & Ball No. 291	Farrow & Ball · Modern Emulsion	матовая	1	73	20,3 м²
	пол		**KM1**	по образцу	Coswick · Вековые традиции · арт. 1167-4250				20,3 м²
	плинтус		**K8**	Farrow & Ball No. 291	МДФ · в цвет Farrow & Ball	полуглянц.	2	73	14,7 м
4. Прихожая-холл 12,91 м²	стены		**K1**	Farrow & Ball No. 291	Farrow & Ball · Modern Emulsion	матовая	1	73	33,9 м²
	потолок		**K3**	NCS S 0502-Y	Tikkurila · Anti-Reflex 2	глубокомат.	2	95	12,9 м²
	пол		**KM2**	Marvel Travertine	Atlas Concorde · арт. A8UZ				12,9 м²
	плинтус		**K4**	Farrow & Ball No. 291	МДФ · в цвет Farrow & Ball			73	12,6 м
5. Кухня 6,52 м²	стены		**K1**	Farrow & Ball No. 291	Farrow & Ball · Modern Emulsion	матовая	1	73	20,5 м²
	потолок		**K1**	Farrow & Ball No. 291	Farrow & Ball · Modern Emulsion	матовая	1	73	6,5 м²
	пол		**KM1**	по образцу	Coswick · Вековые традиции · арт. 1167-4250				6,5 м²
	плинтус		**K8**	Farrow & Ball No. 291	МДФ · в цвет Farrow & Ball	полуглянц.	2	73	9,4 м
	фартук		**KM3**	тон Paper F497 (тёплый белый)	керамогранит · аналог по хар.				2,0 м²

Допущения и предложения на листе

Основа листа: размеры сняты со скана обмерного плана KV design (см): часть подписей не читается, помещения выровнены по читаемым размерам; контрольный обмер не выполнен (К-1); высота потолка 2650 мм принята по отметкам обмера (Н = 2,50…2,66 м, ригель 2,28 м) — уточнить при обмере (К-2); толщины стен 300 / 120 мм приняты, межквартирная стена и колонны — по скану, не замерены (К-1); разрешённая мощность 15 кВт принята по типовым ТУ; при объединении двух квартир — переоформление ТУ (К-4); подрайон климата не задан — принят не северный (жилые от 2,5 м) (К-8).

Знак «**» — предложение проектировщика, заказчиком не утверждено (согласовать с заказчиком): плинтус пом. 1–5, 7–10, акцент пом. 3, фартук пом. 5 — артикул изделия не выбран: позиция описана характеристиками («аналог по характеристикам»), артикул выбирается при закупке; пол пом. 6, 11 — пирог пола: стяжка 33 мм и обмазочная гидроизоляция добавлены разработчиком проекта; артикул изделия не выбран: позиция описана характеристиками («аналог по характеристикам»), артикул выбирается при закупке.

См. лист открытых вопросов (лист 6, записи К-1, К-2, К-4, К-8).

Примечания

1. Цвет на листе и на экране — ориентир. До покраски — выкрас на объекте: не меньше А3 (или лист ГКЛ), на грунте под эту краску, не на белой шпаклёвке, в 2 слоя; на обороте — код, бренд, веер, дата. Смотреть днём и вечером, рядом с образцами пола и плитки. Красить только в цвет утверждённого выкраса.
2. Краску заказывать по коду из графы «Система и код цвета» у бренда этого кода, не «аналогом» другого; весь объём одного кода — одной партией, колеруемую краску — за один проход машины.
3. Площади — те же, что в ведомости отделки (лист 54); сколько краски заказать — в спецификации отделочных материалов (лист 59).
4. Колерная карта на 2 листах: обозначения — на каждом, схема и палитра — на первом, выкрасы — на последнем.

Схема квартиры: цвет стен и акценты (б/м)


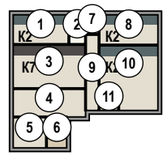


Схема палитры проекта


Стиль: Мид-сенчури 65% + Ар-деко 35% · схема: комплементарная

основной	основной	второстепенный	второстепенный	второстепенный	акцентный	акцентный	акцентный	акцентный
Farrow & Ball No. 291	NCS S 0502-Y	Farrow & Ball No. 298	Farrow & Ball No. 289	Farrow & Ball No. 255	NCS S 2050-Y20R	NCS S 3050-Y70R	NCS S 5030-B10G	NCS S 5040-B90G
School House White — тёплый меловой белый LRV 73 стены 1,3,4,5,8,9,10; плинтус 1,3,4,5,8,9,10; потолок 3,5; текстиль/декор 3	Белый с лёгкой желтизной LRV 95 потолок 1,2,4,6,7,8,9,10,11; стены 2,7; плинтус 2,7; текстиль/декор 1,8,10	Bancha — оливковый середины века LRV 14 текстиль/декор 3,10	Inchyra Blue — тёмный сине-серый LRV 13 акцент 1,8,10; текстиль/декор 1,8,10	Tanner's Brown — тёмный шоколад LRV 7 акцент 3; текстиль/декор 3	Горчичный LRV 42 текстиль/декор 1,8	Терракотовый / жжёный оранжевый LRV 18 текстиль/декор 1,8	Тил LRV 12 текстиль/декор 8	Изумрудный LRV 8 в отделке не применён

План 60/30/10

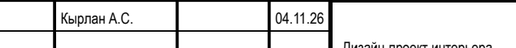

Окраска, факт — по площади стен, акцентов, потолков

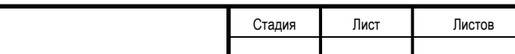

окрашено всего 357 м²; второстепенный тон несут мебель и текстиль

Текстиль и декор в цветах вне палитры проекта

NCS S 1005-Y20R Светлый кремовый — пом. 1 (T7), 3 (T1, T4), 5 (T14), 8 (T11), 10 (T19, T22)

Условные обозначения

- **K1** Farrow & Ball No. 291 · School House White — тёплый меловой белый · Modern Emulsion · матовая · кл. 1
- **K2** Farrow & Ball No. 289 · Inchyra Blue — тёмный сине-серый · Modern Emulsion · матовая · кл. 1
- **K3** NCS S 0502-Y · Белый с лёгкой желтизной · Tikkurila Anti-Reflex 2 · глубокомат. · кл. 2
- **K4** Farrow & Ball No. 291 · School House White — тёплый меловой белый · МДФ
- **K5** NCS S 0502-Y · Белый с лёгкой желтизной · Tikkurila Harmony · матовая · кл. 1
- **K6** NCS S 0502-Y · Белый с лёгкой желтизной · МДФ
- **K7** Farrow & Ball No. 255 · Tanner's Brown — тёмный шоколад · Modern Emulsion · матовая · кл. 1
- дерево (доска, паркет, ламинат) — рисунок досок
- керамогранит, плитка, камень — сетка швов по формату
- **K8** Farrow & Ball No. 291 · School House White — тёплый меловой белый · МДФ · полуглянц. · кл. 2
- **K9** NCS S 0502-Y · Белый с лёгкой желтизной · Tikkurila Luja 7 · матовая · кл. 1
- **KM1** инженерная доска · 1167-4250
- **KM2** керамогранит · A8UZ
- **KM3** аналог: керамогранит матовый, тон F497, 600×600×9 мм
- **KM4** плитка · A8UZ
- **KM5** керамогранит · Atlas Concorde Marvel Travertine Sand — Cross 60×60 Matte Sensitech, арт. AFUL (той же коллекции, что стены A8UZ; тон сверить по образцу)

К — краска, КМ — отделочный материал (тон КМ — по описанию, эталон — образец материала); кл. — класс истирания (1 — самый стойкий к мытью); LRV — светлота цвета: 0 — чёрный, 100 — белый

Изм.	Кол.уч	Лист	№ док.	Подп.	Дата
Разраб.		Кырлан А.С.			04.11.26
Пров.					
ГИП					
Н. контр.					
Утв.					

ГД-2026-009-АИ

Квартира 103 м²

Общая площадь 100,72* м² · * размеры со скана, не замерены (реестр — л. 6, 7, К-1)

Дизайн-проект интерьера

Стадия	Лист	Листов
РП	57	120

Колерная карта

М б/м

Кырлан Александр Сергеевич

выпуск 04.11.2026 № 20cec94f32 · стр. 64 из 130

Колерная карта

Цвета и материалы по помещениям · выкрасы на согласование · лист 2 из 2

Колерная карта по помещениям (продолжение)

Помещение	Поверхность	Образец	Поз.	Система и код цвета	Производитель, линейка / материал, артикул	Блеск	Класс истирания	LRV	Площадь
6. Ванная 3,91 м²	стены		**КМ4**	Marvel Travertine	Atlas Concorde · арт. A8UZ				18,0 м²
	потолок		**К9**	NCS S 0502-Y	Tikkurila · Luja 7	матовая	1	95	3,9 м²
	пол		**КМ5**	по образцу	керамогранит · Atlas Concorde Marvel Travertine Sand Cross 60×60 Matte Sensitech, арт. AFUL (той же коллекции, что стены A8UZ; тон сверить по образцу)				3,9 м²
7. Постирочная 1,51 м²	стены		**К5**	NCS S 0502-Y	Tikkurila · Harmony	матовая	1	95	11,9 м²
	потолок		**К3**	NCS S 0502-Y	Tikkurila · Anti-Reflex 2	глубокомат.	2	95	1,5 м²
	пол		**КМ1**	по образцу	Coswick · Вековые традиции · арт. 1167-4250				1,5 м²
	плинтус		**К6**	NCS S 0502-Y	МДФ · в цвет NCS			95	4,3 м
8. Спальня 2 11,42 м²	стены		**К1**	Farrow & Ball No. 291	Farrow & Ball · Modern Emulsion	матовая	1	73	20,9 м²
	акцент А		**К2**	Farrow & Ball No. 289	Farrow & Ball · Modern Emulsion	матовая	1	13	12,1 м²
	потолок		**К3**	NCS S 0502-Y	Tikkurila · Anti-Reflex 2	глубокомат.	2	95	11,4 м²
	пол		**КМ1**	по образцу	Coswick · Вековые традиции · арт. 1167-4250				11,4 м²
	плинтус		**К4**	Farrow & Ball No. 291	МДФ · в цвет Farrow & Ball			73	13,6 м
9. Коридор 6,02 м²	стены		**К1**	Farrow & Ball No. 291	Farrow & Ball · Modern Emulsion	матовая	1	73	29,2 м²
	потолок		**К3**	NCS S 0502-Y	Tikkurila · Anti-Reflex 2	глубокомат.	2	95	6,0 м²
	пол		**КМ1**	по образцу	Coswick · Вековые традиции · арт. 1167-4250				6,0 м²
	плинтус		**К4**	Farrow & Ball No. 291	МДФ · в цвет Farrow & Ball			73	10,8 м
10. Спальня мастер 22,48 м²	стены		**К1**	Farrow & Ball No. 291	Farrow & Ball · Modern Emulsion	матовая	1	73	31,5 м²
	акцент А		**К2**	Farrow & Ball No. 289	Farrow & Ball · Modern Emulsion	матовая	1	13	12,1 м²
	потолок		**К3**	NCS S 0502-Y	Tikkurila · Anti-Reflex 2	глубокомат.	2	95	22,5 м²
	пол		**КМ1**	по образцу	Coswick · Вековые традиции · арт. 1167-4250				22,5 м²
	плинтус		**К4**	Farrow & Ball No. 291	МДФ · в цвет Farrow & Ball			73	18,5 м
11. Ванная мастер 2,13 м²	стены		**КМ4**	Marvel Travertine	Atlas Concorde · арт. A8UZ				12,6 м²
	потолок		**К9**	NCS S 0502-Y	Tikkurila · Luja 7	матовая	1	95	2,1 м²
	пол		**КМ5**	по образцу	керамогранит · Atlas Concorde Marvel Travertine Sand Cross 60×60 Matte Sensitech, арт. AFUL (той же коллекции, что стены A8UZ; тон сверить по образцу)				2,1 м²

Условные обозначения

- **К1** — Farrow & Ball No. 291 · School House White — тёплый меловой белый · Modern Emulsion · матовая · кл. 1
- **К2** — Farrow & Ball No. 289 · Inchyra Blue — тёмный сине-серый · Modern Emulsion · матовая · кл. 1
- **К3** — NCS S 0502-Y · Белый с лёгкой желтизной · Tikkurila Anti-Reflex 2 · глубокомат. · кл. 2
- **К4** — Farrow & Ball No. 291 · School House White — тёплый меловой белый · МДФ
- **К5** — NCS S 0502-Y · Белый с лёгкой желтизной · Tikkurila Harmony · матовая · кл. 1
- **К6** — NCS S 0502-Y · Белый с лёгкой желтизной · МДФ
- **К7** — Farrow & Ball No. 255 · Tanner's Brown — тёмный шоколад · Modern Emulsion · матовая · кл. 1
- дерево (доска, паркет, ламинат) — рисунок досок
- керамогранит, плитка, камень — сетка швов по формату
- **К8** — Farrow & Ball No. 291 · School House White — тёплый меловой белый · МДФ · полуглянц. · кл. 2
- **К9** — NCS S 0502-Y · Белый с лёгкой желтизной · Tikkurila Luja 7 · матовая · кл. 1
- **КМ1** — инженерная доска · 1167-4250
- **КМ2** — керамогранит · A8UZ
- **КМ3** — аналог: керамогранит матовый, тон F497, 600×600×9 мм
- **КМ4** — плитка · A8UZ
- **КМ5** — керамогранит · Atlas Concorde Marvel Travertine Sand Cross 60×60 Matte Sensitech, арт. AFUL (той же коллекции, что стены A8UZ; тон сверить по образцу)

К — краска, КМ — отделочный материал (тон КМ — по описанию, эталон — образец материала); кл. — класс истирания (1 — самый стойкий к мытью); LRV — светлота цвета: 0 — чёрный, 100 — белый

Перечень выкрасов на согласование

№	Код	Бренд / веер	Пом. / стена	Подложка	Формат	Статус
1	No. 291	Farrow & Ball	1, 3, 4, 5, 8, 9, 10	ГКЛ с грунтом; МДФ под эмаль	600×1000; 300×600	к выполнению
2	No. 289	Farrow & Ball	1 А, 8 А, 10 А	ГКЛ с грунтом	600×1000	к выполнению
3	S 0502-Y	NCS Tikkurila	1, 2, 4, 6, 7, 8, 9, 10, 11	ГКЛ с грунтом; МДФ под эмаль	600×1000; 300×600	к выполнению
4	No. 255	Farrow & Ball	3 А	ГКЛ с грунтом	600×1000	к выполнению

Допущения и предложения на листе

Основа листа: размеры сняты со скана обмерного плана KV design (см): часть подписей не читается, помещения выровнены по читаемым размерам; контрольный обмер не выполнен (К-1); высота потолка 2650 мм принята по отметкам обмера (Н = 2,50…2,66 м, ригель 2,28 м) — уточнить при обмере (К-2); толщины стен 300 / 120 мм приняты, межквартирная стена и колонны — по скану, не замерены (К-1); разрешённая мощность 15 кВт принята по типовым ТУ; при объединении двух квартир — переоформление ТУ (К-4); подрайон климата не задан — принят не северный (жилые от 2,5 м) (К-8).

Знак «**» — предложение проектировщика, заказчиком не утверждено (согласовать с заказчиком): плинтус пом. 1–5, 7–10, акцент пом. 3, фартук пом. 5 — артикул изделия не выбран: позиция описана характеристиками («аналог по характеристикам»), артикул выбирается при закупке; пол пом. 6, 11 — пирог пола: стяжка 33 мм и обмазочная гидроизоляция добавлены разработчиком проекта; артикул изделия не выбран: позиция описана характеристиками («аналог по характеристикам»), артикул выбирается при закупке.

См. лист открытых вопросов (лист 6, записи К-1, К-2, К-4, К-8).

Примечания

1. Цвет на листе и на экране — ориентир. До покраски — выкрас на объекте: не меньше А3 (или лист ГКЛ), на грунте под эту краску, не на белой шпаклёвке, в 2 слоя; на обороте — код, бренд, веер, дата. Смотреть днём и вечером, рядом с образцами пола и плитки; к основному цвету стен — ещё 2 соседних оттенка. Красить только в цвет утверждённого выкраса.
2. Краску заказывать по коду из графы «Система и код цвета» у бренда этого кода, не «аналогом» другого; весь объём одного кода — одной партией, колеруемую краску — за один проход машины.
3. Площади — те же, что в ведомости отделки (лист 54); сколько краски заказать — в спецификации отделочных материалов (лист 59).
4. Колерная карта на 2 листах: обозначения — на каждом, схема и палитра — на первом, выкрасы — на последнем.

Изм.	Кол.уч	Лист	№ док.	Подп.	Дата			
Разраб.		Кырлан А.С.			04.11.26	ГД-2026-009-АИ		
Пров.						Квартира 103 м²		
ГИП						Общая площадь 100,72* м² · * размеры со скана, не замерены (реестр — л. 6, 7, К-1)		
						Дизайн-проект интерьера	Стадия: РП; Лист: 58; Листов: 120	
Н. контр.						Колерная карта	Кырлан Александр Сергеевич	
Утв.						М б/м		

выпуск 04.11.2026 № 20cec94f32 · стр. 65 из 130

Спецификация отделочных материалов

ПРЕДВАРИТЕЛЬНО · не для производства работ · открыто пунктов: 8 (реестр — л. 6, 7)

Форма 1 по ГОСТ 21.110-2013 · количества — из геометрии проекта, с запасом · часть 1 из 2

Поз.	Наименование и техническая характеристика	Тип, марка, обозначение документа	Код продукции	Поставщик	Ед. изм.	Кол.	Масса 1 ед., кг	Примечание
	Лакокрасочные материалы							
1	Краска интерьерная водно-дисперсионная акриловая для стен и потолков, матовая, класс мокрого истирания 1 по EN 13300, база A; цвет по вееру Farrow & Ball No. 291 «School House White — тёплый меловой белый», колеровка машинная	Farrow & Ball Modern Emulsion		Farrow & Ball	л	55		поз. К1 колерной карты; пом. 1, 3, 4, 5, 8, 9, 10; S = 206,3 м² × 2 сл. × 0,12 л/м² = 49,5 л, +10 % и 0,5 л на подкраску → ≥ 55,0 л; тара 11 × 5 л
2	Краска интерьерная водно-дисперсионная акриловая для акцентных стен, матовая, класс мокрого истирания 1 по EN 13300, база C; цвет по вееру Farrow & Ball No. 289 «Inchyra Blue — тёмный сине-серый», колеровка машинная	Farrow & Ball Modern Emulsion		Farrow & Ball	л	10		поз. К2 колерной карты; пом. 1, 8, 10; S = 35,6 м² × 2 сл. × 0,12 л/м² = 8,5 л, +10 % и 0,5 л на подкраску → ≥ 9,9 л; тара 2 × 5 л
3	Краска интерьерная водно-дисперсионная акриловая для потолков, глубокоматовая, класс мокрого истирания 2 по EN 13300, база A; цвет NCS S 0502-Y «Белый с лёгкой желтизной», колеровка машинная	Tikkurila Anti-Reflex 2		Tikkurila	л	18,9		поз. К3 колерной карты; пом. 1, 2, 4, 7, 8, 9, 10; S = 67,8 м² × 2 сл. × 0,12 л/м² = 16,3 л, +10 % и 0,5 л на подкраску → ≥ 18,4 л; тара 2 × 9 л + 1 × 0,9 л
4	Краска интерьерная водно-дисперсионная акриловая для стен, матовая, класс мокрого истирания 1 по EN 13300, база A; цвет NCS S 0502-Y «Белый с лёгкой желтизной», колеровка машинная	Tikkurila Harmony		Tikkurila	л	9		поз. К5 колерной карты; пом. 2, 7; S = 29,5 м² × 2 сл. × 0,12 л/м² = 7,1 л, +10 % и 0,5 л на подкраску → ≥ 8,3 л; тара 1 × 9 л
5	Краска интерьерная водно-дисперсионная акриловая для акцентных стен, матовая, класс мокрого истирания 1 по EN 13300, база C; цвет по вееру Farrow & Ball No. 255 «Tanner's Brown — тёмный шоколад», колеровка машинная	Farrow & Ball Modern Emulsion		Farrow & Ball	л	7,5		поз. К7 колерной карты; пом. 3; S = 11,7 м² × 3 сл. × 0,12 л/м² = 4,2 л, +10 % и 0,5 л на подкраску → ≥ 5,1 л; тара 1 × 5 л + 1 × 2,5 л
6	Краска интерьерная водно-дисперсионная акриловая для потолков, матовая, класс мокрого истирания 1 по EN 13300, база A; цвет NCS S 0502-Y «Белый с лёгкой желтизной», колеровка машинная	Tikkurila Luja 7		Tikkurila	л	2,7		поз. К9 колерной карты; пом. 6, 11; S = 6,0 м² × 2 сл. × 0,12 л/м² = 1,4 л, +10 % и 0,5 л на подкраску → ≥ 2,1 л; тара 1 × 2,7 л
7	Краска для МДФ и дерева в цвет Farrow & Ball No. 291 «School House White — тёплый меловой белый» — окраска плинтуса; блеск не ниже блеска стен	марка не задана			л	2,4		поз. К4, К8; пом. 1, 3, 4, 5, 8, 9, 10; L = 92,6 м, S = 9,1 м² × 2 сл. × 0,12 л/м² + 10 %; продукт подобрать в веере Farrow & Ball
8	Краска для МДФ и дерева в цвет NCS S 0502-Y «Белый с лёгкой желтизной» — окраска плинтуса; блеск не ниже блеска стен	марка не задана			л	0,5		поз. К6; пом. 2, 7; L = 10,8 м, S = 1,1 м² × 2 сл. × 0,12 л/м² + 10 %; продукт подобрать в веере NCS
9	Грунтовка акриловая под окраску стен и потолков — из системы производителя краски	по системе краски			м²	357		площадь окраски стен, акцентов и потолков; 1 слой перед окраской; расход — по ТУ грунтовки

Допущения и предложения на листе

Основа листа: размеры сняты со скана обмерного плана KV design (см): часть подписей не читается, помещения выровнены по читаемым размерам; контрольный обмер не выполнен (К-1); высота потолка 2650 мм принята по отметкам обмера (Н = 2,50…2,66 м, ригель 2,28 м) — уточнить при обмере (К-2); толщины стен 300 / 120 мм приняты, межквартирная стена и колонны — по скану, не замерены (К-1); разрешённая мощность 15 кВт принята по типовым ТУ; при объединении двух квартир — переоформление ТУ (К-4); подрайон климата не задан — принят не северный (жилые от 2,5 м) (К-8).

Знак «**» — предложение проектировщика, заказчиком не утверждено (согласовать с заказчиком): плинтус пом. 1–5, 7–10, акцент пом. 3, фартук пом. 5 — артикул изделия не выбран: позиция описана характеристиками («аналог по характеристикам»), артикул выбирается при закупке; пол пом. 6, 11 — пирог пола: стяжка 33 мм и обмазочная гидроизоляция добавлены разработчиком проекта; артикул изделия не выбран: позиция описана характеристиками («аналог по характеристикам»), артикул выбирается при закупке.

Изменения по листу без подписи: ИЗ-1.

См. лист открытых вопросов (лист 6, записи ИЗ-1, К-1, К-2, К-4, К-8).

Изм.	Кол.уч	Лист	№ док.	Подп.	Дата
Разраб.		Кырлан А.С.			04.11.26
Пров.					
ГИП					
Н. контр.					
Утв.					

ГД-2026-009-АИ

Квартира 103 м²

Общая площадь 100,72* м² · * размеры со скана, не замерены (реестр — л. 6, 7, К-1)

Дизайн-проект интерьера

Стадия	Лист	Листов
РП	59	120

Спецификация отделочных материалов

М б/м

Кырлан Александр Сергеевич

Спецификация отделочных материалов

ПРЕДВАРИТЕЛЬНО · не для производства работ · открыто пунктов: 8 (реестр — л. 6, 7)

Форма 1 по ГОСТ 21.110-2013 · количества — из геометрии проекта, с запасом · часть 2 из 2

Поз.	Наименование и техническая характеристика	Тип, марка, обозначение документа	Код продукции	Поставщик	Ед. изм.	Кол.	Масса 1 ед., кг	Примечание
	Плитка и керамогранит							
10	Atlas Concorde Marvel Travertine Sand Cross 60×60 Matte Sensitech, арт. AFUL (той же коллекции, что стены A8UZ; тон сверить по образцу), 600×600×9 мм, ректификат, водопоглощение 0,1 % (BIa), противоскольжение R10, PEI IV	Atlas Concorde Marvel Travertine Sand Cross 60×60 Matte Sensitech, арт. AFUL (той же коллекции, что стены A8UZ; тон сверить по образцу)			м²	9,36		шов 2 мм; Ванная, пол; Ванная мастер, пол; по раскладке 23 шт (S = 6,04 м²), с запасом 26 шт
11	A8UZ, 600×1200×9 мм, ректификат, водопоглощение 0,1 % (BIa), противоскольжение R10, PEI IV	A8UZ		Atlas Concorde	м²	70,56		шов 2 мм; Ванная, стены А–Г; Ванная, короб инсталляции; Ванная мастер, стены А–Г; Ванная мастер, короб инсталляции; Прихожая-холл, пол; по раскладке 86 шт (S = 45,03 м²), с запасом 98 шт
12	Керамогранит матовый, тон F497, ректификат, водопоглощение 0,5 % (BIa)	аналог по характеристикам			м²	2,22		5. Кухня, фартук; раскладка не выполнена — S = 2,01 м² + 10 %; клей и затирка — по раскладке
	Напольные покрытия							
13	1167-4250, рабочий слой 4 мм, эмиссия E1, укладка на клей	1167-4250		Coswick	м²	87,5		пом. 1, 2, 3, 5, 7, 8, 9, 10; S = 81,77 м² + 7 % (прямая укладка); к заказу — кратно упаковке
14	Клей для паркета и инженерной доски, эластичный (СМП / полиуретановый)	по рекомендации производителя доски			м²	82		площадь приклейки; расход и шпатель — по ТУ клея
	Погонажные изделия							
15	Ultrawood Base 5340, ЛДФ под окраску, 83×15 мм, 2440 мм (арт. LDF-BASE-5340), крепление к стене, окраска в цвет Farrow & Ball No. 291	Ultrawood Base 5340, ЛДФ под окраску, 83×15 мм, 2440 мм (арт. LDF-BASE-5340)			м	102		пом. 1, 3, 4, 5, 8, 9, 10; L = 92,6 м (периметр без дверных проёмов) + 10 % на подрезку; в штуках — по длине планки
16	Ultrawood Base 5340, ЛДФ под окраску, 83×15 мм, 2440 мм (арт. LDF-BASE-5340), крепление к стене, окраска в цвет NCS S 0502-Y	Ultrawood Base 5340, ЛДФ под окраску, 83×15 мм, 2440 мм (арт. LDF-BASE-5340)			м	12		пом. 2, 7; L = 10,8 м (периметр без дверных проёмов) + 10 % на подрезку; в штуках — по длине планки
	Смеси и материалы для облицовки							
17	Затирка для швов плитки, класс CG2WA по EN 13888	Mapei Ultracolor Plus 132		Mapei	кг	4		по раскладке (a+b)/(a·b) × шов × t × 1,6 + 10 %; в т. ч. 1,0 кг — позиции раскладки без марки
18	Клей плиточный C2 TE S1 по EN 12004, слой 5 мм	Ceresit CM 17		Ceresit	кг	402		17 меш. по 25 кг; 1,5 кг/м² на 1 мм слоя + 10 %; в т. ч. 105 кг — позиции раскладки без марки
19	Гидроизоляция обмазочная мокрых зон: пол, стены по периметру, зоны замачивания; 2 слоя с армирующей лентой в углах	аналог по характеристикам			м²	18,7		площадь по листу раскладки плитки + 10 %; расход смеси — по ТУ
20	Лента демпферная по периметру пола из плитки	аналог по характеристикам			м	27,1		периметр без дверных проёмов + 10 %

Примечания

1. Количества — из геометрии проекта: площади поверхностей по чистым граням стен до отделки (те же, что в ведомости отделки и колерной карте), плитка, клей и затирка — по раскладке плиточника; в графе «Кол.» — к заказу, с запасом.
2. Краска: расход 0,12 л/м² на слой в 2 слоя, если по ТУ не задан иной; запас 10 % и 0,5 л на подкраску каждого кода. Один код — одна партия, колеровка машинная в колеровочном центре бренда; в заказ — только после утверждения выкраса (колерная карта). Фасовка — по каталогу бренда на дату выпуска; к заказу — не меньше расчётного объёма.
3. «Аналог по характеристикам» — допускается изделие другого производителя с характеристиками не ниже указанных, по согласованию с автором проекта.
4. Графы «Код продукции» и «Масса 1 ед.» не заполнены: коды по классификатору продукции не присвоены, масса единицы до 25 кг (ГОСТ 21.110-2013).
5. Грунтовка и клей для доски указаны площадью обработки; объём — по ТУ выбранного продукта.

Допущения и предложения на листе

Основа листа: размеры сняты со скана обмерного плана KV design (см): часть подписей не читается, помещения выровнены по читаемым размерам; контрольный обмер не выполнен (К-1); высота потолка 2650 мм принята по отметкам обмера (H = 2,50…2,66 м, ригель 2,28 м) — уточнить при обмере (К-2); толщины стен 300 / 120 мм приняты, межквартирная стена и колонны — по скану, не замерены (К-1); разрешённая мощность 15 кВт принята по типовым ТУ; при объединении двух квартир — переоформление ТУ (К-4); подрайон климата не задан — принят не северный (жилые от 2,5 м) (К-8).

Знак «**» — предложение проектировщика, заказчиком не утверждено (согласовать с заказчиком): плинтус пом. 1–5, 7–10, акцент пом. 3, фартук пом. 5 — артикул изделия не выбран: позиция описана характеристиками («аналог по характеристикам»), артикул выбирается при закупке; пол пом. 6, 11 — пирог пола: стяжка 33 мм и обмазочная гидроизоляция добавлены разработчиком проекта; артикул изделия не выбран: позиция описана характеристиками («аналог по характеристикам»), артикул выбирается при закупке.

См. лист открытых вопросов (лист 6, записи К-1, К-2, К-4, К-8).

Изм.	Кол.уч	Лист	№ док.	Подп.	Дата
Разраб.		Кырлан А.С.			04.11.26
Пров.					
ГИП					
Н. контр.					
Утв.					

ГД-2026-009-АИ

Квартира 103 м²

Общая площадь 100,72* м² · * размеры со скана, не замерены (реестр — л. 6, 7, К-1)

Дизайн-проект интерьера

Стадия	Лист	Листов
РП	60	120

Спецификация отделочных материалов

М б/м

Кырлан Александр Сергеевич

Концепция декора и визуализации

Мид-сенчури · ретро с авторской мебелью · визуализации, палитра, материалы, ключевые предметы



Визуализация 1. Вид сверху (3D): планировка с мебелью, текстилем и декором

Расстановка — по плану мебели (лист 19); шторы, ковры, картины и растения — по плану текстиля и декора (лист 62).

Материалы и фактуры




Дуб натуральный
пол: пом. 1, 2, 3, 5, 7, 8, 9, 10; рамы ДК3, ДК4, ДК7



Букле
подушки: Т10, Т16



Лён
портьеры, подушки, рулонная: Т1, Т4, Т7, Т11, Т14, Т19, Т22

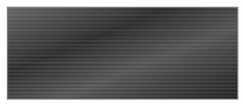

Чёрный матовый металл
рамы ДК5, ДК6 — чёрный



Бархат
подушки: Т5, Т17, Т23

Ключевые предметы


— Диван Г2 2600×900 — гостиная-столовая; подушки и плед Т4, Т5, Т6
— Кровати М1, С1 — над изголовьем картины ДК4, ДК7; текстиль Т16, Т17, Т18, Т22, Т23, Т24
— Ковры Т3, Т9, Т15, Т21 — шерсть, на противоскользящей подложке
— Картины ДК1, ДК3, ДК4, ДК7 — центр на высоте 1450–1650 мм
— Зеркала в рост ДК5, ДК6
— Шторы-волна Т1, Т7, Т11, Т19 (NCS S 1005-Y20R), тюль Т2, Т8, Т13, Т20 (NCS S 0502-Y) — в нишах потолка
— Растение ДК2, растение ДК9

Настроение

Ретро 2026: модернизм середины века 65 % + ар-деко 35 %. Стены — School House White No. 291, потолки — белый S 0502-Y; второй план — орех и тик, оливковый Bancha No. 298, сине-серый Inchyra Blue No. 289; акценты — горчица S 2050-Y20R, терракота S 3050-Y70R, тил S 5030-B10G, изумрудный бархат S 5040-B90G; металл — латунь. Мебель — авторские модели середины века (как предложение, модели уточняются с заказчиком). Настроение стиля: оптимизм, функциональность, тёплое дерево, лёгкость, ретро без китча, связь с улицей, графичные акценты. Свет тёплый, 2700–3000 K.

Примечания


1. Визуализации — образ интерьера. Изделия, размеры, высоты подвеса и привязки — по чертежам (план текстиля и декора — лист 62; шторы и карнизы — лист 63; ведомость текстиля — лист 64; ведомость декора и развеска — лист 65); при расхождении действуют чертежи и ведомости.
2. Коды цвета — ориентир подбора по веерам производителей; ткань утверждается по образцу при дневном свете и при свете проекта 2700–3000 K.
3. Мелкий стайлинг на визуализациях (книги, посуда, свечи) в ведомости не входит и поставляется заказчиком по желанию.

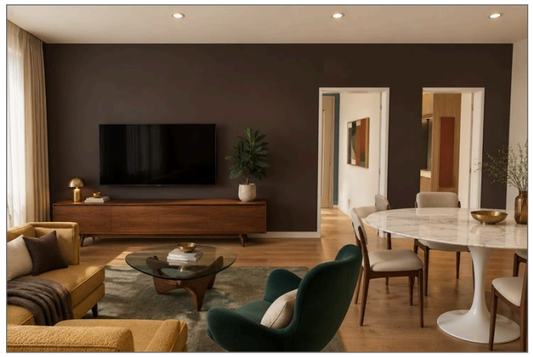

Визуализация 18. Гостиная-столовая (пом. 3)
шторы Т1, Т2 · ковёр Т3 · картина ДК1 · растение ДК2 · подушки, пледы Т4, Т5, Т6



Визуализация 16. Кухня (пом. 5)
шторы Т14 · растение ДК9

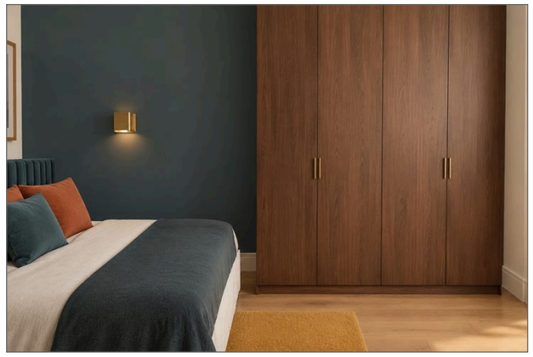

Визуализация 6. Спальня 2 (пом. 8)
шторы Т11, Т13 · ковёр Т15 · картина ДК4 · зеркало ДК6 · подушки, пледы Т16, Т17, Т18



Визуализация 9. Спальня мастер (пом. 10)
шторы Т19, Т20 · ковёр Т21 · картина ДК7 · подушки, пледы Т22, Т23, Т24

Палитра 60/30/10 и цвета текстиля



- Farrow & Ball No. 291 (School House White — тёплый меловой белый), LRV 73 — 60 % база — Т2
- NCS S 0502-Y (Белый с лёгкой желтизной), LRV 95 — 60 % база — Т8, Т13, Т20
- Farrow & Ball No. 298 (Bancha — оливковый середины века), LRV 14 — 30 % второй цвет — Т3, Т21
- Farrow & Ball No. 289 (Inchyra Blue — тёмный сине-серый), LRV 13 — 30 % второй цвет — Т12, Т18, Т23, Т24
- Farrow & Ball No. 255 (Tanner's Brown — тёмный шоколад), LRV 7 — 30 % второй цвет — Т5, Т6
- NCS S 2050-Y20R (Горчичный), LRV 42 — 10 % акцент — Т9, Т15
- NCS S 3050-Y70R (Терракотовый / жжёный оранжевый), LRV 18 — 10 % акцент — Т10, Т16
- NCS S 5030-B10G (Тил), LRV 12 — 10 % акцент — Т17
- NCS S 5040-B90G (Изумрудный), LRV 8 — 10 % акцент
- NCS S 1005-Y20R (Светлый кремовый), LRV 77 — текстиль — Т1, Т4, Т7, Т11, Т14, Т19, Т22

Допущения и предложения на листе. Основа листа: размеры сняты со скана обмерного плана KV design (см): часть подписей не читается, помещения выровнены по читаемым размерам; контрольный обмер не выполнен (К-1); высота потолка 2650 мм принята по отметкам обмера (Н = 2,50…2,66 м, ригель 2,28 м) — уточнить при обмере (К-2); толщины стен 300 / 120 мм приняты, межквартирная стена и колонны — по скану, не замерены (К-1); разрешённая мощность 15 кВт принята по типовым ТУ; при объединении двух квартир — переоформление ТУ (К-4); подрайон климата не задан — принят не северный (жилые от 2,5 м) (К-8). См. лист открытых вопросов (лист 6, записи К-1, К-2, К-4, К-8).

Изм.	Кол.уч	Лист	№ док.	Подп.	Дата
Разраб.		Кырлан А.С.			04.11.26
Пров.					
ГИП					
Н. контр.					
Утв.					

ГД-2026-009-АИ

Квартира 103 м²

Общая площадь 100,72* м² · * размеры со скана, не замерены (реестр — л. 6, 7, К-1)

Дизайн-проект интерьера

Стадия	Лист	Листов
РП	61	120

Концепция декора и визуализации

М б/м


Кырлан Александр Сергеевич

выпуск 04.11.2026 № 20cec94f32 · стр. 68 из 130

План текстиля и декора

Шторы и карнизы, ковры, картины и зеркала, растения · размеры в мм от чистовых стен и чистого пола · марки — по ведомостям

ПРЕДВАРИТЕЛЬНО · не для производства работ · открыто пунктов: 8 (реестр — л. 6, 7)

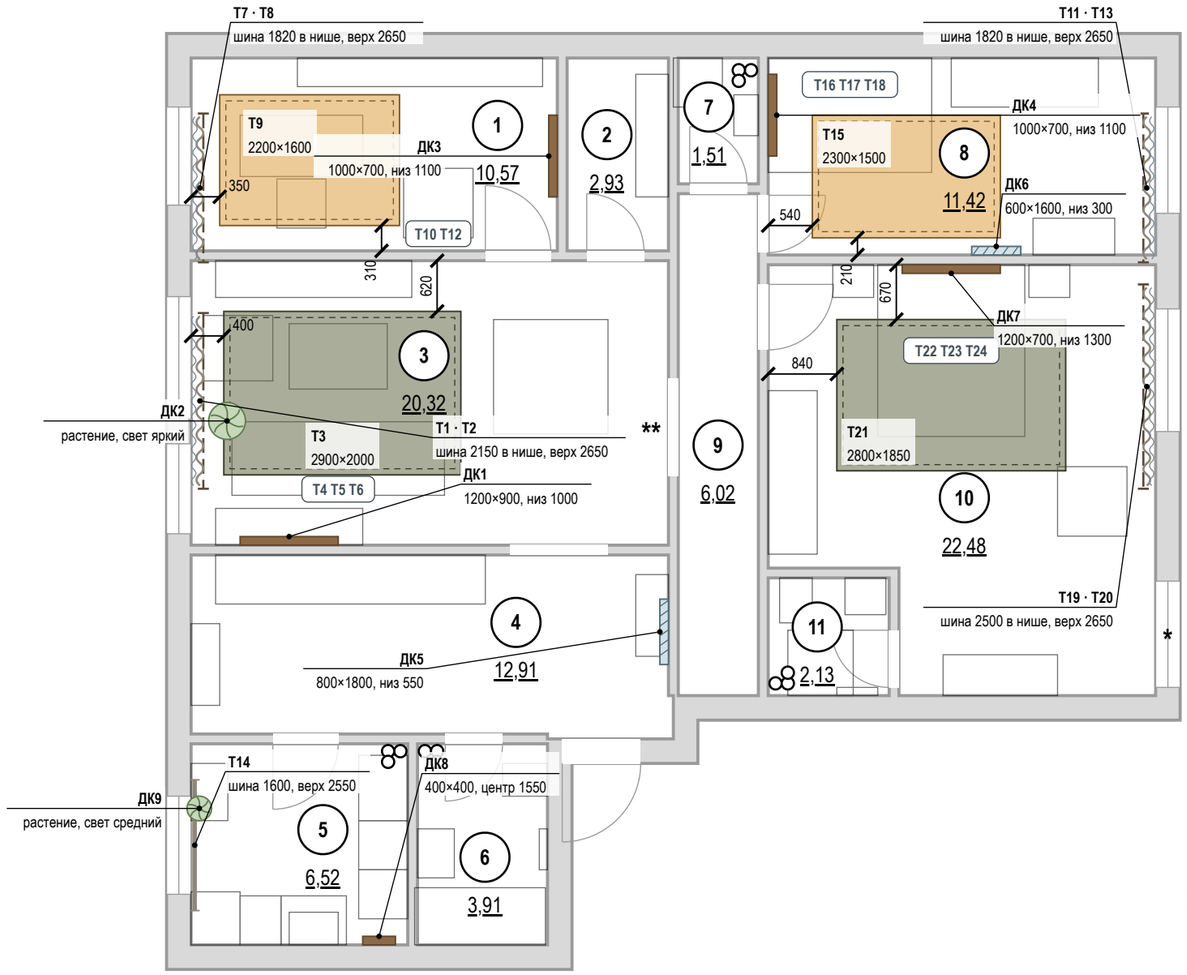

Условные обозначения

- ковёр — габарит в масштабе, цвет изделия
- шина или карниз штор (выше плоскости разреза)
- портьеры (штора-волна)
- тюль (на плане — волнистая линия)
- римская или рулонная штора в проёме
- картина на стене — ширина в масштабе
- зеркало на стене — ширина в масштабе
- растение в кашпо — диаметр в масштабе
- ваза, настольный декор
- подушки, пледы — марки на мебели
- привязка от чистовой стены, мм
- (1) номер помещения, площадь м²
- стены (подложка обмера)
- * «*» — принято, не замерено и не подтверждено
- ** «**» — предложение проектировщика, заказчиком не утверждено

Т1, ДК1 — марки по ведомостям текстиля и декора

Экспликация помещений

лист 14 · на плане — номера в марках

Окна: шина → полотно, мм

Поз.	Шина	Верх шины	Полотно, низ
Т7, Т8	1820	2650, ниша	2640, низ 10
Т1, Т2	2150	2650, ниша	2640, низ 10
Т14	1600	2550	1750, низ 800
Т11, Т13	1820	2650, ниша	2640, низ 10
Т19, Т20	2500	2650, ниша	2640, низ 10

Допущения и предложения на листе

Основа листа: размеры сняты со скана обмерного плана KV design (см): часть подписей не читается, помещения выровнены по читаемым размерам; контрольный обмер не выполнен (К-1); высота потолка 2650 мм принята по отметкам обмера (Н = 2,50…2,66 м, ригель 2,28 м) — уточнить при обмере (К-2); толщины стен 300 / 120 мм приняты, межквартирная стена и колонны — по скану, не замерены (К-1); разрешённая мощность 15 кВт принята по типовым ТУ; при объединении двух квартир — переоформление ТУ (К-4); подрайон климата не задан — принят не северный (жилые от 2,5 м) (К-8).

Знак «*» — принято, не замерено и не подтверждено (замерить на объекте): К-1: окно пом. 10 (стена Б) — Окно 1300 при offset 3500 на стене Б основной части (длина 3830) выходило за стену на 970 мм; К-6: Ст К1-3, Ст В1-3, Ст Т3-3 — положение снято со скана обмера, отдельно не замерялось; ось внутри габарита поддона См1 — обмер угла по К-6.

Знак «**» — предложение проектировщика, заказчиком не утверждено (согласовать с заказчиком): К-5: дверь пом. 3 (стена Б) — проём в межквартирной стене — объединение квартир, предложение до техзаключения.

См. лист открытых вопросов (лист 6, записи К-1, К-2, К-4–К-6, К-8).

Примечания

1. Размеры — в мм. Отступы ковров — от чистовых стен; высоты картин и зеркал — от чистого пола до центра или низа рамы.
2. Шторы — на шинах в нишах потолка (ниша — план потолков, лист 45); закладная под шину — до обшивки ГКЛ. Схемы окон, длины полотен и сборка — лист 63.
3. Картины и зеркала массой более 5 кг — на анкеры по основанию, нагрузка крепежа не меньше двойной массы изделия; на ГКЛ — только по закладной. Декор не перекрывает розетки и выключатели.
4. Ковры на гладком полу — на противоскользящей подложке.
5. Мебель — по плану расстановки мебели (лист 19); ведомость текстиля — лист 64, ведомость декора и схемы развески — лист 65.
6. Знак «*» у проёма — допущение: положение проёма не замерено (окно пом. 10, стена Б); размер напечатан как принятый. Реестр: листы 6–7, вопрос К-1.
7. Номера помещений — по экспликации (лист 14); наименования и площади на этом листе не дублируются.
8. Марки текстиля «Т» и декора «Д» относятся только к листам текстиля и декора; индексы трубопроводов Т1–Т4 — на листах ВК и ОВ.

1000 мм · печать 1:1

Изм.	Кол.уч	Лист	№ док.	Подп.	Дата
Разраб.		Кырлан А.С.			04.11.26
Пров.					
ГИП					
Н. контр.					
Утв.					

ГД-2026-009-АИ

Квартира 103 м²

Общая площадь 100,72* м² · * размеры со скана, не замерены (реестр — л. 6, 7, К-1)

Дизайн-проект интерьера

Стадия	Лист	Листов
РП	62	120

План текстиля и декора

М 1:75

Кырлан Александр Сергеевич

выпуск 04.11.2026 № 20cec94f32 · стр. 69 из 130

08

Декор и текстиль


Кырлан Александр Сергеевич

выпуск 04.11.2026 № 20cec94f32 · стр. 70 из 130


Шторы и карнизы

Схемы окон «шина → полотно» (М 1:100) · отметки от чистого пола помещения · размеры в мм


Окно 1 — Кабинет-библиотека (пом. 1): Т7, Т8 (М 1:100)

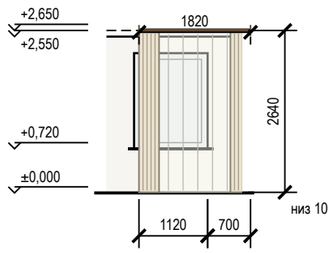


Окно 1 — Гостиная-столовая (пом. 3): Т1, Т2 (М 1:100)

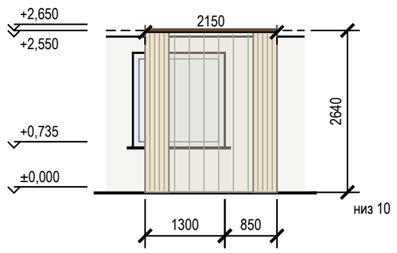


Окно 1 — Кухня (пом. 5): Т14 (М 1:100)

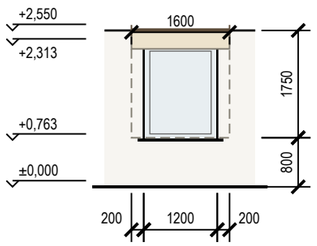

Окно 1 — Спальня 2 (пом. 8): Т11, Т13 (М 1:100)

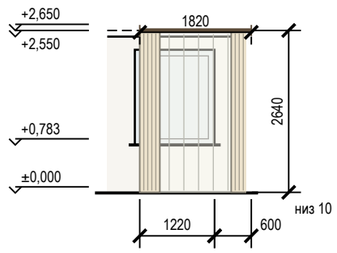

Окно 1 — Спальня мастер (пом. 10): Т19, Т20 (М 1:100)

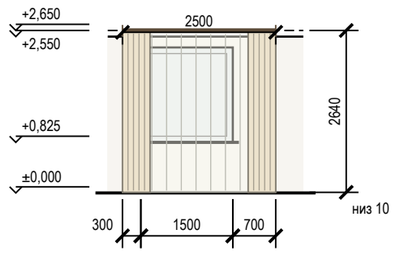

Карта окон: окно → шина → полотно

Поз.	Окно, пом.	Проём Ш×В, подоконник	Верх ниши	Изделие	Шина / карниз: длина, крепление	Верх шины	Полотно: длина, низ	Управление
Т7	1, пом. 1	1200×1560, подок. 720	+2,650	портьеры	шина, 1820, в нише потолка, вынос 150	+2,650	2640, низ 10 (парит)	вручную
Т8	1, пом. 1	1200×1560, подок. 720	+2,650	тюль	шина, 1820, в нише потолка, вынос 150	+2,650	2640, низ 10 (парит)	вручную
Т1	1, пом. 3	1500×1550, подок. 735	+2,650	портьеры	шина, 2150, в нише потолка, вынос 150	+2,650	2640, низ 10 (парит)	вручную
Т2	1, пом. 3	1500×1550, подок. 735	+2,650	тюль	шина, 2150, в нише потолка, вынос 100	+2,650	2640, низ 10 (парит)	вручную
Т14	1, пом. 5	1200×1550, подок. 763		рулонная штора	шина, 1600, на потолок, вынос 120	+2,550	1750, низ 800	без шнура
Т11	1, пом. 8	1300×1552, подок. 783	+2,650	портьеры	шина, 1820, в нише потолка, вынос 150	+2,650	2640, низ 10 (парит)	вручную
Т13	1, пом. 8	1300×1552, подок. 783	+2,650	тюль	шина, 1820, в нише потолка, вынос 150	+2,650	2640, низ 10 (парит)	вручную
Т19	1, пом. 10	1500×1548, подок. 825	+2,650	портьеры	шина, 2500, в нише потолка, вынос 150	+2,650	2640, низ 10 (парит)	вручную
Т20	1, пом. 10	1500×1548, подок. 825	+2,650	тюль	шина, 2500, в нише потолка, вынос 150	+2,650	2640, низ 10 (парит)	вручную

Задания смежникам

Кому	Задание	Пом.
Гипсокартонщик	окно 1 (1200×1560, Т7, Т8): ниша под шторы 150×100, верх +2,650; закладная под шину L 1820 по всей длине — до обшивки	1
Гипсокартонщик	окно 1 (1500×1550, Т1, Т2): ниша под шторы 150×100, верх +2,650; закладная под шину L 2150 по всей длине — до обшивки	3
Гипсокартонщик	окно 1 (1300×1552, Т11, Т13): ниша под шторы 150×100, верх +2,650; закладная под шину L 1820 по всей длине — до обшивки	8
Гипсокартонщик	окно 1 (1500×1548, Т19, Т20): ниша под шторы 150×100, верх +2,650; закладная под шину L 2500 по всей длине — до обшивки	10
Электрик	выводы под электрокарнизы не требуются (управление вручную)	

Условные обозначения

- портьеры в открытом положении
- римская штора: сложена / опущена
- верх ниши под шторы в потолке
- тюль (на виде окна — прозрачная плашка)
- шина или карниз на отметке верха
- оконный проём

Допущения и предложения на листе

Основа листа: размеры сняты со скана обмерного плана KV design (см): часть подписей не читается, помещения выровнены по читаемым размерам; контрольный обмер не выполнен (К-1); высота потолка 2650 мм принята по отметкам обмера (Н = 2,50…2,66 м, ригель 2,28 м) — уточнить при обмере (К-2); толщины стен 300 / 120 мм приняты, межквартирная стена и колонны — по скану, не замерены (К-1); разрешённая мощность 15 кВт принята по типовым ТУ; при объединении двух квартир — переоформление ТУ (К-4); подрайон климата не задан — принят не северный (жилые от 2,5 м) (К-8).

Знак «*» — принято, не замерено и не подтверждено (замерить на объекте): К-1: окно пом. 10 (стена Б) — Окно 1300 при offset 3500 на стене Б основной части (длина 3830) выходило за стену на 970 мм.

Знак «**» — предложение проектировщика, заказчиком не утверждено (согласовать с заказчиком): К-5: дверь пом. 3 (стена Б) — проём в межквартирной стене — объединение квартир, предложение до техзаключения.

См. лист открытых вопросов (лист 6, записи К-1, К-2, К-4, К-5, К-8).

Примечания

1. Отметки — от чистого пола помещения; размеры — мм.
2. Шины в нишах потолка: закладная (брус или профиль) по всей длине ниши — до обшивки ГКЛ; ниша и её отметка — узел ниши на плане потолков (лист 45).
3. Шина в нише — на отметке верха ниши (крепление к закладной в потолке ниши); длина полотна — от верха шины до чистого пола за вычетом зазора.
4. Полотно портьер «парит» над полом на 10 мм; сборка портьер — 2,0, тюля — 2,5 (ширина полотна — в ведомости текстиля).
5. Шнур римской шторы — с натяжителем, петля низом не ниже 1500 мм от пола (защита детей; EN 13120 — рекомендация).
6. Электрокарнизы не предусмотрены; при замене на электропривод — вывод кабеля в нише у края шины (задание электрику).
7. Марки изделий — по плану текстиля и декора (лист 62) и ведомости текстиля (лист 64).

Изм.	Кол.уч	Лист	№ док.	Подп.	Дата
Разраб.		Кырлан А.С.			04.11.26
Пров.					
ГИП					
Н. контр.					
Утв.					

ГД-2026-009-АИ

Квартира 103 м²

Общая площадь 100,72* м² · * размеры со скана, не замерены (реестр — л. 6, 7, К-1)

Дизайн-проект интерьера

Стадия	Лист	Листов
РП	63	120

Шторы и карнизы

М б/м

Кырлан Александр Сергеевич

выпуск 04.11.2026 № 20cec94f32 · стр. 71 из 130

Ведомость текстиля

Шторы, тюль, римские шторы, ковры, подушки и пледы · размеры в мм · марки — по плану текстиля и декора

Текстиль: шторы, ковры, подушки, пледы

Поз.	Пом.	Изделие	Размер, мм	Ткань, состав, плотность	Сборка, ширина полотна		Цвет (система, код)	Кол.	Примечание
T1	3	Портьеры-волна, два полотна	шина 2150 × полотно 2640	лён 100 %; 280 г/м²	× 2, ширина 4300		NCS S 1005-Y20R (Светлый кремовый)	2	низ 10 (парит); в нише потолка; уход: химчистка; отпаривание на карнизе
T2	3	Тюль-вуаль, одно полотно	шина 2150 × полотно 2640	вуаль; полиэстер 100 %; 60 г/м²	× 2,5, ширина 5375		Farrow & Ball No. 291 (School House White тёплый меловой белый)	1	низ 10 (парит); в нише потолка; уход: стирка 30 °C, вешать влажной
T3	3	Ковёр мягкой группы, абстрактная геометрия середины века	2900×2000	шерсть, плоское плетение; шерсть 100 %			Farrow & Ball No. 298 (Bancha — оливковый середины века)	1	противоскользящая подложка; ворс 8 мм; уход: сухая чистка, пылесос без турбощётки
T4	3	Подушки декоративные на диван	500×500	лён 100 %			NCS S 1005-Y20R (Светлый кремовый)	3	на Г2; уход: съёмный чехол, стирка 30 °C
T5	3	Подушки декоративные на диван, акцент	400×600	хлопковый бархат 100 %			Farrow & Ball No. 255 (Tanner's Brown — тёмный шоколад)	2	на Г2; уход: химчистка
T6	3	Плед на диван	1300×1700	шерсть мериноса 100 %			Farrow & Ball No. 255 (Tanner's Brown — тёмный шоколад)	1	на Г2; уход: ручная стирка 30 °C
T7	1	Портьеры-волна	шина 1820 × полотно 2640	лён с блэкаут-подкладкой; лён 100 %; 320 г/м²	× 2, ширина 3640		NCS S 1005-Y20R (Светлый кремовый)	2	низ 10 (парит); в нише потолка
T8	1	Тюль	шина 1820 × полотно 2640	вуаль; полиэстер 100 %	× 2,5, ширина 4550		NCS S 0502-Y (Белый с лёгкой желтизной)	1	низ 10 (парит); в нише потолка
T9	1	Ковёр под рабочей зоной, геометрия середины века	2200×1600	шерсть, плоское плетение; шерсть 100 %			NCS S 2050-Y20R (Горчичный)	1	противоскользящая подложка; ворс 8 мм
T10	1	Подушки декоративные на кровать	500×500	букле (шерсть 60 %, полиэстер 40 %)			NCS S 3050-Y70R (Терракотовый / жжёный оранжевый)	3	на Б4
T11	8	Портьеры-волна	шина 1820 × полотно 2640	лён с блэкаут-подкладкой; лён 100 %; 320 г/м²	× 2, ширина 3640		NCS S 1005-Y20R (Светлый кремовый)	2	низ 10 (парит); в нише потолка
T12	1	Плед на кровать	1300×1700	шерсть мериноса 100 %			Farrow & Ball No. 289 (Inchyra Blue — тёмный сине-серый)	1	на Б4
T13	8	Тюль	шина 1820 × полотно 2640	вуаль; полиэстер 100 %	× 2,5, ширина 4550		NCS S 0502-Y (Белый с лёгкой желтизной)	1	низ 10 (парит); в нише потолка
T14	5	Рулонная штора кассетная, ткань димаут	шина 1600 × полотно 1750	ткань димаут с грязеотталкивающей пропиткой; полиэстер 100 %			NCS S 1005-Y20R (Светлый кремовый)	1	низ 800; на потолок; шнур: петля —, cordless; уход: протирка влажной губкой
T15	8	Ковёр под кроватью	2300×1500	шерсть, плоское плетение; шерсть 100 %			NCS S 2050-Y20R (Горчичный)	1	противоскользящая подложка; ворс 8 мм
T16	8	Подушки декоративные на кровать	500×500	букле (шерсть 60 %, полиэстер 40 %)			NCS S 3050-Y70R (Терракотовый / жжёный оранжевый)	3	на С1
T17	8	Подушки на кровать, акцент	400×600	хлопковый бархат 100 %			NCS S 5030-B10G (Тил)	2	на С1
T18	8	Плед на кровать	1300×1700	шерсть мериноса 100 %			Farrow & Ball No. 289 (Inchyra Blue — тёмный сине-серый)	1	на С1
T19	10	Портьеры-волна	шина 2500 × полотно 2640	лён с блэкаут-подкладкой; лён 100 %; 320 г/м²	× 2, ширина 5000		NCS S 1005-Y20R (Светлый кремовый)	2	низ 10 (парит); в нише потолка
T20	10	Тюль	шина 2500 × полотно 2640	вуаль; полиэстер 100 %	× 2,5, ширина 6250		NCS S 0502-Y (Белый с лёгкой желтизной)	1	низ 10 (парит); в нише потолка
T21	10	Ковёр под кроватью	2800×1850	шерсть, ручное ткачество; шерсть 80 %, хлопок 20 %			Farrow & Ball No. 298 (Bancha — оливковый середины века)	1	противоскользящая подложка; ворс 10 мм
T22	10	Подушки декоративные на кровать	500×500	лён 100 %			NCS S 1005-Y20R (Светлый кремовый)	3	на М1
T23	10	Подушки на кровать, акцент	400×600	хлопковый бархат 100 %			Farrow & Ball No. 289 (Inchyra Blue — тёмный сине-серый)	2	на М1
T24	10	Плед на кровать	1300×1700	шерсть мериноса 100 %			Farrow & Ball No. 289 (Inchyra Blue — тёмный сине-серый)	1	на М1

образец цвета — по HEX производителя краски, справочно

Итого: шторы и тюль — 13 шт.; ковры и дорожки — 4 шт.; подушки, пледы, покрывала — 22 шт.

Примечания

1. Коды цвета — ориентир подбора по веерам производителей красок; ткань утверждается по образцу при дневном свете и при свете проекта 2700–3000 K.
2. Размеры полотен — по замеру после чистовой отделки пола и потолка; ширина полотна указана с учётом сборки, без припусков на швы. Схемы окон и отметки шин лист 63.
3. Портьеры и тюль — на тесьме «волна» по системе шины; блэкаут — подкладкой. Ковры — на противоскользящей подложке.
4. Замена изделия — аналогом по характеристикам (состав, плотность, размер, цвет по образцу) с согласованием автора проекта.
5. Места изделий — план текстиля и декора (лист 62); подушки и пледы — по марке мебели.

Допущения и предложения на листе

Основа листа: размеры сняты со скана обмерного плана KV design (см): часть подписей не читается, помещения выровнены по читаемым размерам; контрольный обмер не выполнен (К-1); высота потолка 2650 мм принята по отметкам обмера (Н = 2,50…2,66 м, ригель 2,28 м) — уточнить при обмере (К-2); толщины стен 300 / 120 мм приняты, межквартирная стена и колонны — по скану, не замерены (К-1); разрешённая мощность 15 кВт принята по типовым ТУ; при объединении двух квартир — переоформление ТУ (К-4); подрайон климата не задан — принят не северный (жилые от 2,5 м) (К-8).
См. лист открытых вопросов (лист 6, записи К-1, К-2, К-4, К-8).

Изм.	Кол.уч	Лист	№ док.	Подп.	Дата
Разраб.		Кырлан А.С.			04.11.26
Пров.					
ГИП					
Н. контр.					
Утв.					

ГД-2026-009-АИ

Квартира 103 м²

Общая площадь 100,72* м² · * размеры со скана, не замерены (реестр — л. 6, 7, К-1)

Дизайн-проект интерьера

Стадия	Лист	Листов
РП	64	120

Ведомость текстиля

М б/м

Кырлан Александр Сергеевич

выпуск 04.11.2026 № 20cec94f32 · стр. 72 из 130

Ведомость декора. Схемы развески


Картины, зеркала, растения, настольный декор · схемы развески (М 1:50) · высоты — мм от чистого пола

Декор: картины, зеркала, растения, предметы


картина · зеркало · мебель под изделием

Поз.	Пом.	Предмет	Размер, мм	Место: стена, высота от пола, мм	Масса, кг	Крепёж и основание	Свет места, отделка	Кол.
ДК1	3	Картина над буфетом: Песочные и грейжевые поля, холст	1200×900	стена В, привязка 600; низ 1000, центр 1450; над Г6	6	планка на дюбелях, 4 точки; основание: перегородка 120 мм; нагрузка 20 кг		1
ДК2	3	Фикус лировидный в кашпо Ø400	450×450	напольное			свет яркий рассеянный	1
ДК3	1	Картина над креслом: Горизонт над полем, карандаш	1000×700	стена Б, привязка 700; низ 1100, центр 1450; над Б4	4	подвес по основанию, 2 точки	рама — дуб	1
ДК4	8	Картина над кроватью: Горизонт над полем, карандаш	1000×700	стена Г, привязка 200; низ 1100, центр 1450; над С1	4	подвес по основанию, 2 точки	рама — дуб	1
ДК5	4	Зеркало	800×1800	стена Б, привязка 540; низ 550, центр 1450	18	анкер, 4 шт.; основание: перегородка — определить обмером до монтажа; нагрузка 40 кг	рама — чёрный матовый металл	1
ДК6	8	Зеркало в рост в тонкой чёрной раме	600×1600	стена В, привязка 2490; низ 300, центр 1100	12	анкер для пустотелых оснований, 4 шт.; основание: перегородка — определить обмером до монтажа; нагрузка 30 кг	рама — чёрный матовый металл	1
ДК7	10	Картина над кроватью: Серо-синяя абстракция, холст	1200×700	стена А, привязка 1640; низ 1300, центр 1650; над М1	4	подвес по основанию, 2 точки	рама — дуб	1
ДК8	5	Часы настенные Ø400	400×400	стена В, привязка 2100; центр 1550	2	дюбель с крюком, 1 точка; основание: перегородка 120 мм; нагрузка 10 кг		1
ДК9	5	Хлорофитум хохлатый на подоконнике (отм. +0,800)	300×200	напольное			свет средний	1


ДК1 — Гостиная-столовая (пом. 3), стена В (М 1:50)

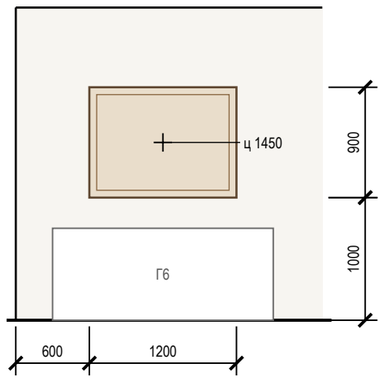


ДК3 — Кабинет-библиотека (пом. 1), стена Б (М 1:50)

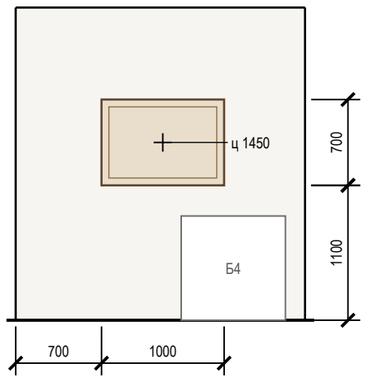


ДК4 — Спальня 2 (пом. 8), стена Г (М 1:50)

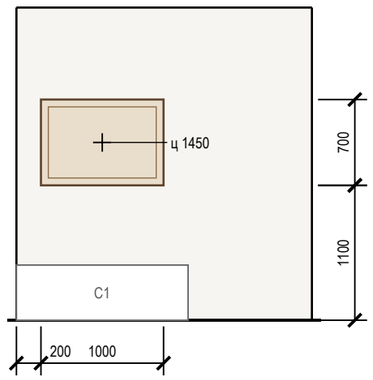


ДК5 — Прихожая-холл (пом. 4), стена Б (М 1:50)

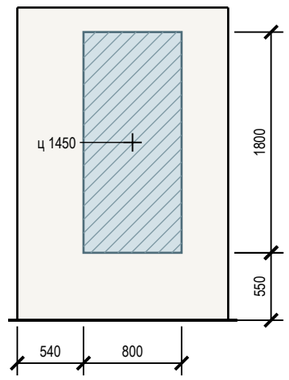


ДК6 — Спальня 2 (пом. 8), стена В (М 1:50)

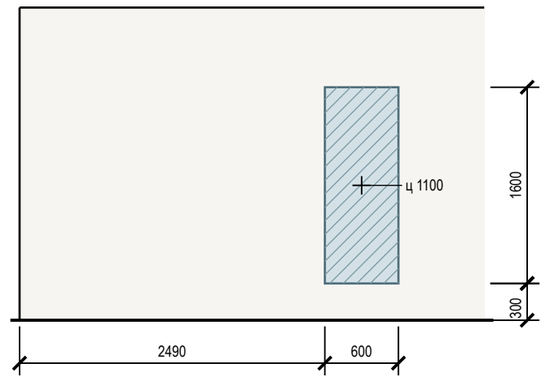

ДК7 — Спальня мастер (пом. 10), стена А (М 1:50)

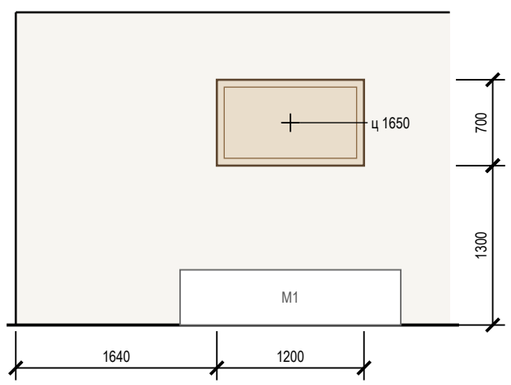

ДК8 — Кухня (пом. 5), стена В (М 1:50)

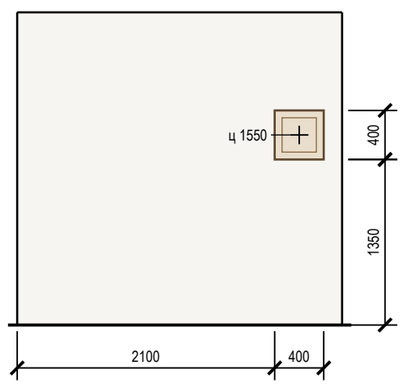

Допущения и предложения на листе

Основа листа: размеры сняты со скана обмерного плана KV design (см): часть подписей не читается, помещения выровнены по читаемым размерам; контрольный обмер не выполнен (К-1); высота потолка 2650 мм принята по отметкам обмера (Н = 2,50…2,66 м, ригель 2,28 м) — уточнить при обмере (К-2); толщины стен 300 / 120 мм приняты, межквартирная стена и колонны — по скану, не замерены (К-1); разрешённая мощность 15 кВт принята по типовым ТУ; при объединении двух квартир — переоформление ТУ (К-4); подрайон климата не задан — принят не северный (жилые от 2,5 м) (К-8).

См. лист открытых вопросов (лист 6, записи К-1, К-2, К-4, К-8).

Примечания

1. Высоты — от чистого пола помещения до низа изделия, «ц» — до центра; привязки — от чистовой грани угла стены, мм.
2. Над мебелью низ изделия — на 150–250 мм выше спинки или изголовья; без мебели центр — на 1450–1600 мм от пола.
3. Изделия до 5 кг — на два подвеса по основанию; тяжелее — на анкеры с нагрузкой не меньше двойной массы; на ГКЛ — только по закладной или анкеру для пустотелых оснований.
4. Зеркала в рост — с креплением от опрокидывания; в санузлах — влагостойкие, на клей для зеркал и нейтральный силикон.
5. Места изделий — план текстиля и декора (лист 62).

Изм.	Кол.уч	Лист	№ док.	Подп.	Дата
Разраб.		Кырлан А.С.			04.11.26
Пров.					
ГИП					
Н. контр.					
Утв.					

ГД-2026-009-АИ

Квартира 103 м²

Общая площадь 100,72* м² · * размеры со скана, не замерены (реестр — л. 6, 7, К-1)

Дизайн-проект интерьера

Стадия	Лист	Листов
РП	65	120

Ведомость декора. Схемы развески

М б/м


Кырлан Александр Сергеевич

выпуск 04.11.2026 № 20cec94f32 · стр. 73 из 130

Встроенная мебель. Схема расположения

встроенная и корпусная мебель на заказ, кухонный гарнитур · размеры в мм · марки — по ведомости изделий

ПРЕДВАРИТЕЛЬНО · не для производства работ · открыто пунктов: 8 (реестр — л. 6, 7)

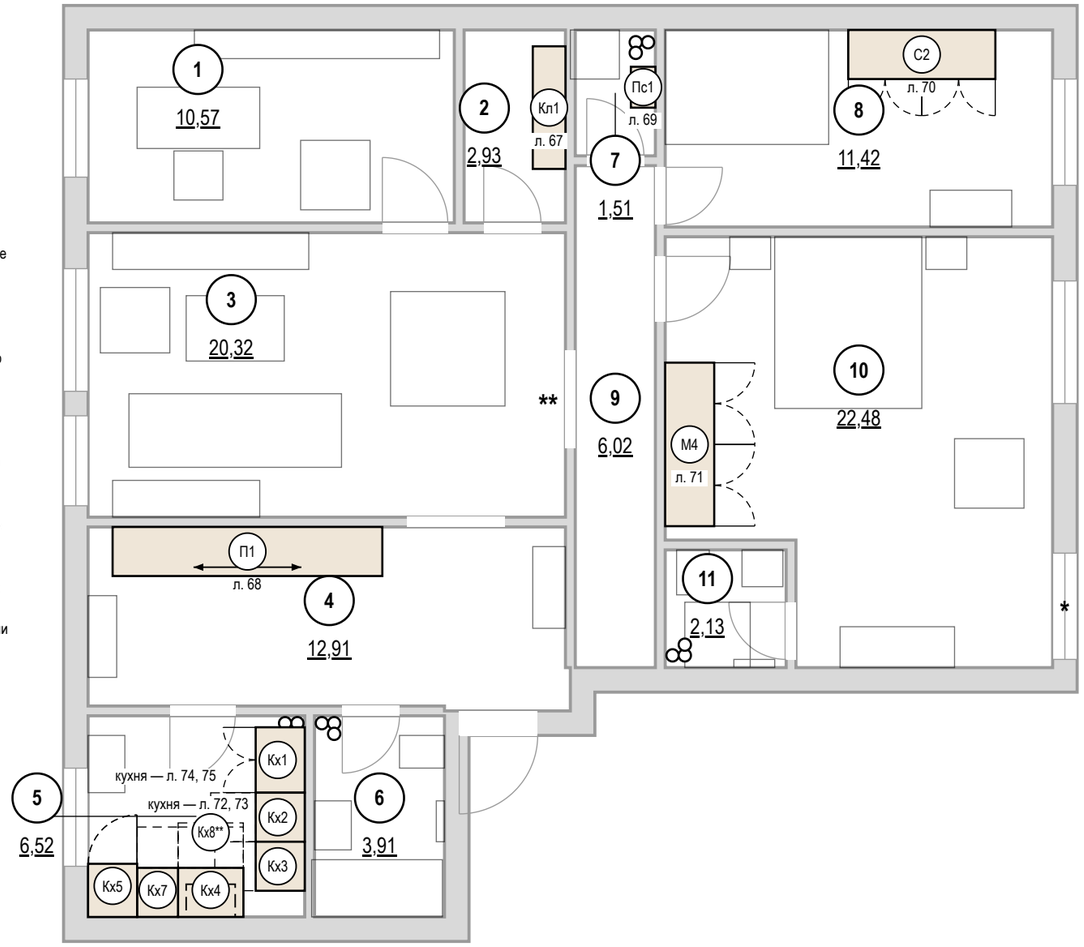

Допущения и предложения на листе

Основа листа: размеры сняты со скана обмерного плана KV design (см): часть подписей не читается, помещения выровнены по читаемым размерам; контрольный обмер не выполнен (К-1); высота потолка 2650 мм принята по отметкам обмера (Н = 2,50…2,66 м, ригель 2,28 м) — уточнить при обмере (К-2); толщины стен 300 / 120 мм приняты, межквартирная стена и колонны — по скану, не замерены (К-1); разрешённая мощность 15 кВт принята по типовым ТУ; при объединении двух квартир — переоформление ТУ (К-4); подрайон климата не задан — принят не северный (жилые от 2,5 м) (К-8).

Знак «*» — принято, не замерено и не подтверждено (замерить на объекте): К-1: окно пом. 10 (стена Б) — Окно 1300 при offset 3500 на стене Б основной части (длина 3830) выходило за стену на 970 мм; К-6: Ст К1-3, Ст В1-3, Ст Т3-3 — положение снято со скана обмера, отдельно не замерялось; ось внутри габарита поддона См1 — обмер угла по К-6.

Знак «**» — предложение проектировщика, заказчиком не утверждено (согласовать с заказчиком): Кх8 — над индукционной панелью Кх4 нужна вытяжка: в составе кухни её не было, розетка вытяжки образца висела без потребителя; К-5: дверь пом. 3 (стена Б) — проём в межквартирной стене — объединение квартир, предложение до техзаключения.

См. лист открытых вопросов (лист 6, записи К-1, К-2, К-4–К-6, К-8).

Ведомость изделий

Марка	Наименование	Пом.	Ш×Г×В, мм	Лист
Кл1	Система хранения	2	1500×400×2400	67
П1	Шкаф-купе	4	3300×600×2450	68
Пс1	Система хранения	7	500×300×2000	69
С2	Шкаф распашной	8	1800×600×2400	70
М4	Шкаф распашной	10	2000×600×2400	71
Кх1	Модуль нижний: мойка	5	800×600×900	72
Кх2	Модуль под ПММ 60: без корпуса, фасад на дверь машины	5	600×600×900	72
Кх3	Модуль нижний: ящики	5	600×600×900	72
Кх4	Модуль нижний: духовой шкаф, варочная	5	800×600×900	74
Кх8**	Модуль навесной: полки	5	600×400×600	74
Кх7	Модуль нижний: ящики	5	500×600×900	74
Кх5	Пенал: холодильник встр.	5	600×650×2100	74

Условные обозначения

- изделие мебельщика: корпус на полу
- невидимый контур: навесной модуль, корпус под столешницей
- открывание распашного фасада
- зона выдвижения ящика, двери техники
- дверь купе, стрелка — направление движения
- К1 — марка изделия или модуля (на схеме расположения под ней — лист изделия)
- * — «*» — принято, не замерено и не подтверждено
- ** — «**» — предложение проектировщика, заказчиком не утверждено

Примечания

1. Изделия — по чистовым размерам помещений; перед раскроем — контрольный замер цеха после чистовой отделки стен, пола и потолка.
2. Открывание фасадов и выдвижение ящиков показано в открытом положении: зоны не пересекают двери, радиаторы, выключатели и проходы.
3. Стояки и счётчики за мебелью — с сервисным люком; газовые трубы мебелью не зашиваются.
4. Покупная мебель — по плану расстановки мебели и спецификации дизайнера; здесь — подложкой.
5. Знак «*» у проёма — положение не замерено; реестр: листы 6–7, вопрос К-1.

1000 мм · печать 1:1

Изм.	Кол.уч	Лист	№ док.	Подп.	Дата
Разраб.		Кырлан А.С.			04.11.26
Пров.					
ГИП					
Н. контр.					
Утв.					

ГД-2026-009-АИ

Квартира 103 м²

Общая площадь 100,72* м² · * размеры со скана, не замерены (реестр — л. 6, 7, К-1)

Дизайн-проект интерьера

Стадия	Лист	Листов
РП	66	120

Встроенная мебель. Схема расположения

М 1:75

Кырлан Александр Сергеевич


выпуск 04.11.2026 № 20cec94f32 · стр. 74 из 130

Система хранения Кл1


Кладовая (пом. 2) · вид из помещения · размеры в мм, отметки в м

ПРЕДВАРИТЕЛЬНО · не для производства работ · открыто пунктов: 8 (реестр — л. 6, 7)


Общий вид

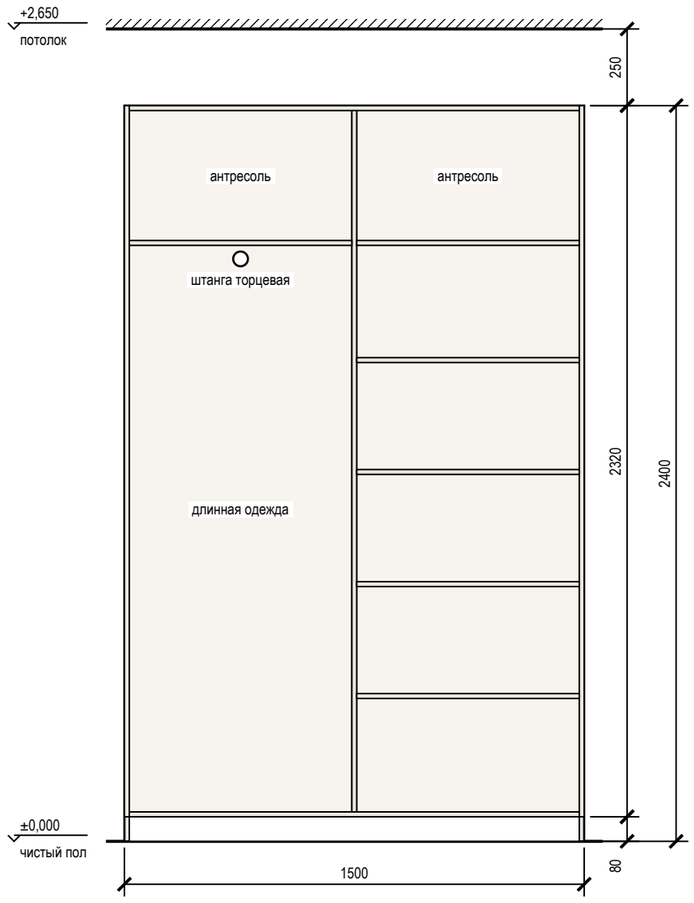


Наполнение, размеры в свету

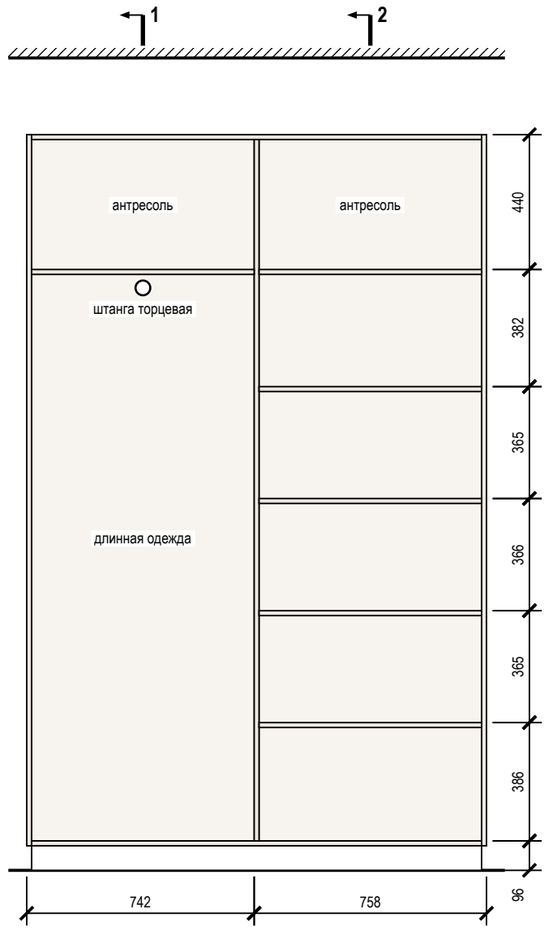

Разрез 1-1

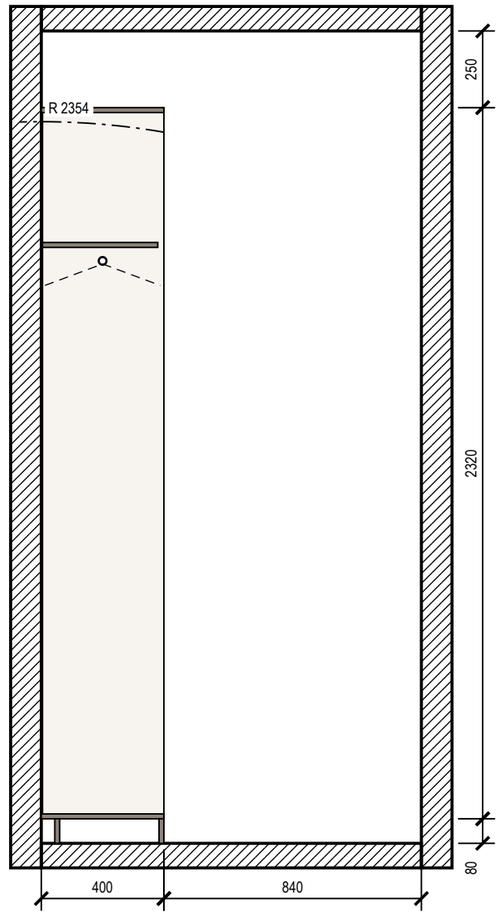

Разрез 2-2

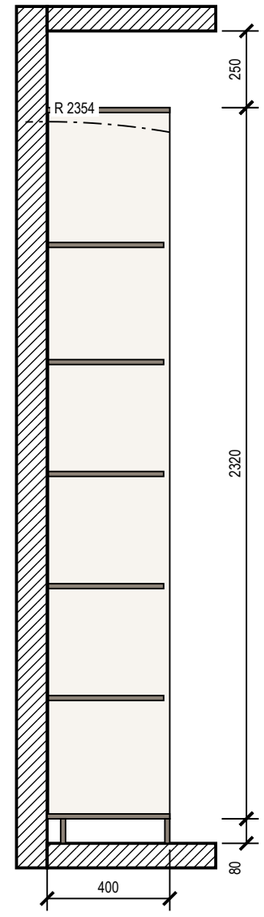

Примечания

1. Размеры — в мм по чистовой отделке; изделие 1500×400×2400 (Ш×Г×В). Перед раскроем — контрольный замер цеха после чистовой отделки стен, пола и потолка.
2. Корпус — ЛДСП декор «орех» 16 мм, задняя стенка ХДФ 4 мм в паз, цоколь 80 мм на регулируемых опорах; открытая система: без фасадов.
3. Кромка: скрытые торцы 0,4 мм, видимые 2 мм (ПВХ/АБС).
4. Присадка по 32-й системе — выполняет цех.
5. Зазор до потолка 250 мм.
6. Подъём корпуса: диагональ боковины без цоколя $\sqrt{(2320^2 + 400^2)} = 2354$ мм < 2650 мм до потолка — корпус собирается лёжа, поднимается поворотом и ставится на цоколь.
7. Крепление к стене от опрокидывания — уголки 2 шт. к несущему основанию (монтажная схема шкафов).
8. Проход перед изделием 840 мм показан на разрезе 1-1.

Условные обозначения

- корпус и полки ЛДСП (вид на стену)
- задняя стенка ХДФ
- деталь в разрезе
- штанга для плечиков (на разрезе — плечики 450 мм)
- траектория угла корпуса при подъёме в проектное положение

Допущения и предложения на листе

Основа листа: размеры сняты со скана обмерного плана KV design (см): часть подписей не читается, помещения выровнены по читаемым размерам; контрольный обмер не выполнен (К-1); высота потолка 2650 мм принята по отметкам обмера (Н = 2,50…2,66 м, ригель 2,28 м) — уточнить при обмере (К-2); толщины стен 300 / 120 мм приняты, межквартирная стена и колонны — по скану, не замерены (К-1); разрешённая мощность 15 кВт принята по типовым ТУ; при объединении двух квартир — переоформление ТУ (К-4); подрайон климата не задан — принят не северный (жилые от 2,5 м) (К-8).
См. лист открытых вопросов (лист 6, записи К-1, К-2, К-4, К-8).

1000 мм · печать 1:1

Изм.	Кол.уч	Лист	№ док.	Подп.	Дата
Разраб.		Кырлан А.С.			04.11.26
Пров.					
ГИП					
Н. контр.					
Утв.					

ГД-2026-009-АИ

Квартира 103 м²

Общая площадь 100,72* м² · * размеры со скана, не замерены (реестр — л. 6, 7, К-1)

Дизайн-проект интерьера

Стадия	Лист	Листов
РП	67	120

Система хранения Кл1

М 1:20


Кырлан Александр Сергеевич

Шкаф-купе П1


Прихожая-холл (пом. 4) · вид из помещения · размеры в мм, отметки в м

ПРЕДВАРИТЕЛЬНО · не для производства работ · открыто пунктов: 8 (реестр — л. 6, 7)


Вид с фасадами

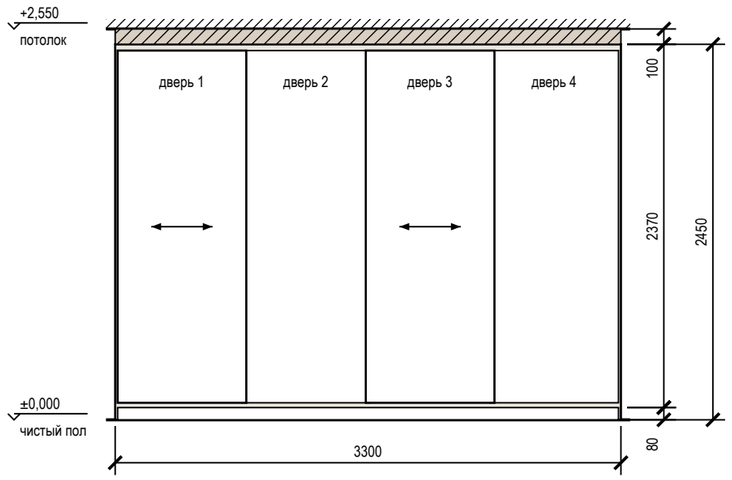


Вид без фасадов

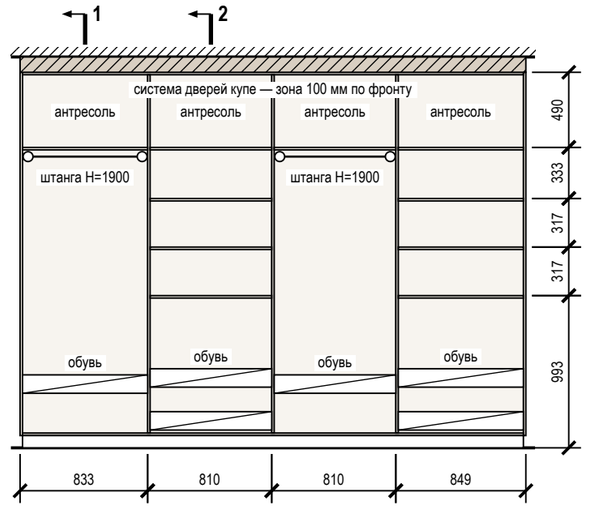

Разрез 1-1

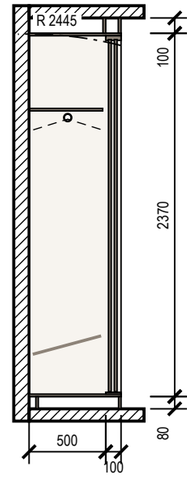

Разрез 2-2

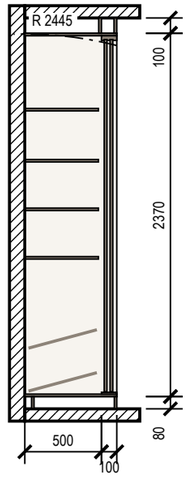

Примечания

1. Размеры — в мм по чистовой отделке; изделие 3300×600×2450 (Ш×Г×В). Перед раскроем — контрольный замер цеха после чистовой отделки стен, пола и потолка.
2. Корпус — ЛДСП 16 мм, задняя стенка ХДФ 4 мм в паз, цоколь 80 мм на регулируемых опорах; двери купе — МДФ, шпон ореха 10 мм, масло матовое в профиле: латунь; нахлёст 30 мм, ширина двери 840 мм, высота — проём минус 40 мм; цвет — по колерной карте.
3. Кромка: скрытые торцы 0,4 мм, видимые 2 мм (ПВХ/АБС).
4. Номинальные зазоры: дверь купе — боковина 3 мм, фасад ящика — стойка 2 мм; ящики внутри купе — с накладкой 30 мм на стойке со стороны нахлёста дверей.
5. Присадка по 32-й системе — выполняет цех.
6. Компенсатор 100 мм — короб из ЛДСП по фронту и торцам, подгоняется к потолку при монтаже (припуск 20 мм), крепится к корпусу и к потолку.
7. Подъём корпуса: диагональ боковины без цоколя $\sqrt{(2370^2 + 600^2)} = 2445$ мм < 2550 мм до потолка — корпус собирается лёжа, поднимается поворотом и ставится на цоколь.
8. Крепление к стене от опрокидывания — уголки 2 шт. к несущему основанию (монтажная схема шкафов).

Условные обозначения

- дверь купе, стрелка — направление движения
- корпус и полки ЛДСП (вид на стену)
- задняя стенка ХДФ
- деталь в разрезе
- компенсатор — короб до потолка
- штанга для плечиков (на разрезе — плечики 450 мм)
- траектория угла корпуса при подъёме в проектное положение

Допущения и предложения на листе

Основа листа: размеры сняты со скана обмерного плана KV design (см): часть подписей не читается, помещения выровнены по читаемым размерам; контрольный обмер не выполнен (К-1); высота потолка 2650 мм принята по отметкам обмера (H = 2,50…2,66 м, ригель 2,28 м) — уточнить при обмере (К-2); толщины стен 300 / 120 мм приняты, межквартирная стена и колонны — по скану, не замерены (К-1); разрешённая мощность 15 кВт принята по типовым ТУ; при объединении двух квартир — переоформление ТУ (К-4); подрайон климата не задан — принят не северный (жилые от 2,5 м) (К-8).

См. лист открытых вопросов (лист 6, записи К-1, К-2, К-4, К-8).

1000 мм · печать 1:1

Изм.	Кол.уч	Лист	№ док.	Подп.	Дата
Разраб.		Кырлан А.С.			04.11.26
Пров.					
ГИП					
Н. контр.					
Утв.					

ГД-2026-009-АИ

Квартира 103 м²

Общая площадь 100,72* м² · * размеры со скана, не замерены (реестр — л. 6, 7, К-1)

Дизайн-проект интерьера

Стадия	Лист	Листов
РП	68	120

Шкаф-купе П1

М 1:40

Кырлан Александр Сергеевич


выпуск 04.11.2026 № 20cec94f32 · стр. 76 из 130

Система хранения Пс1


Постирочная (пом. 7) · вид из помещения · размеры в мм, отметки в м

ПРЕДВАРИТЕЛЬНО · не для производства работ · открыто пунктов: 8 (реестр — л. 6, 7)


Общий вид

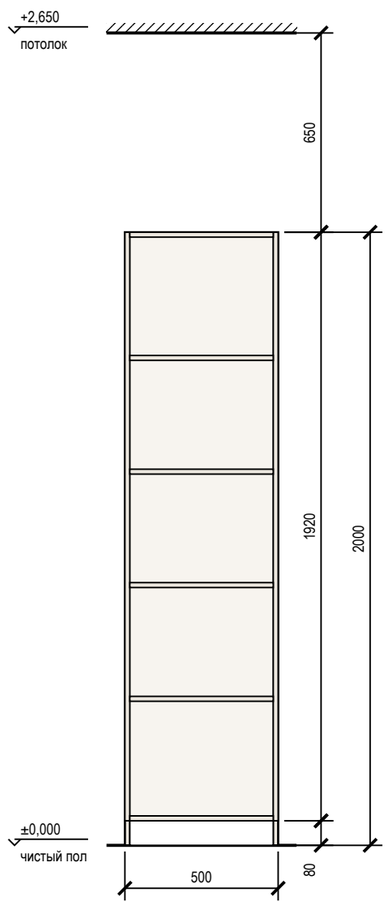

Наполнение, размеры в свету

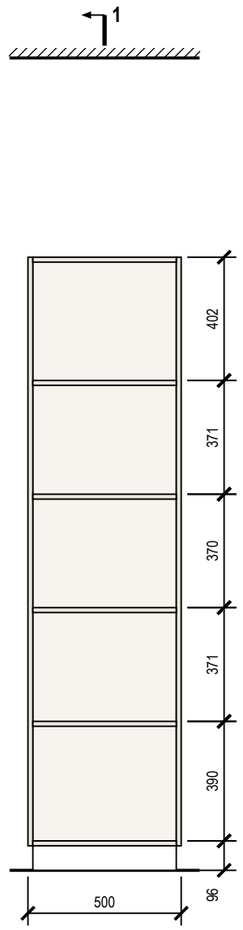

Разрез 1-1

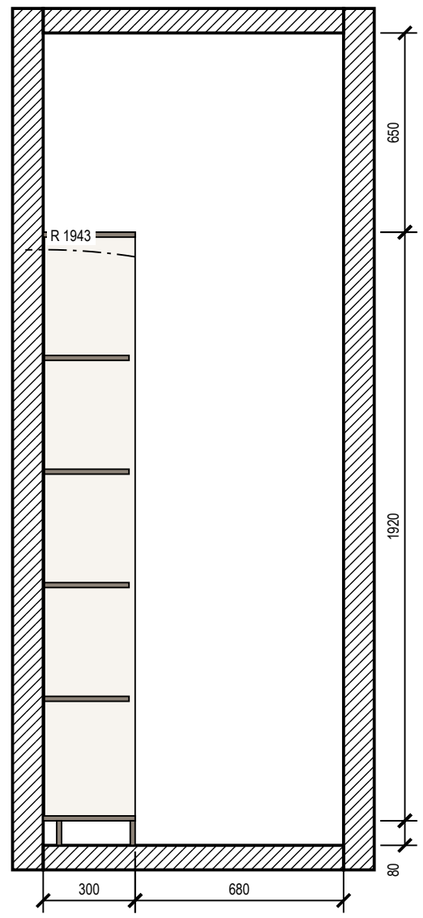

Примечания

1. Размеры — в мм по чистовой отделке; изделие 500×300×2000 (Ш×Г×В). Перед раскроем — контрольный замер цеха после чистовой отделки стен, пола и потолка.
2. Корпус — ЛДСП 16 мм, задняя стенка ХДФ 4 мм в паз, цоколь 80 мм на регулируемых опорах; открытая система: без фасадов.
3. Кромка: скрытые торцы 0,4 мм, видимые 2 мм (ПВХ/АБС).
4. Присадка по 32-й системе — выполняет цех.
5. Зазор до потолка 650 мм.
6. Подъём корпуса: диагональ боковины без цоколя √(1920² + 300²) = 1943 мм < 2650 мм до потолка — корпус собирается лёжа, поднимается поворотом и ставится на цоколь.
7. Крепление к стене от опрокидывания — уголки 2 шт. к несущему основанию (монтажная схема шкафов).
8. Проход перед изделием 680 мм показан на разрезе 1-1.

Условные обозначения

- корпус и полки ЛДСП (вид на стену)
- задняя стенка ХДФ
- деталь в разрезе
- штанга для плечиков (на разрезе — плечики 450 мм)
- траектория угла корпуса при подъёме в проектное положение

Допущения и предложения на листе

Основа листа: размеры сняты со скана обмерного плана KV design (см): часть подписей не читается, помещения выровнены по читаемым размерам; контрольный обмер не выполнен (К-1); высота потолка 2650 мм принята по отметкам обмера (Н = 2,50…2,66 м, ригель 2,28 м) — уточнить при обмере (К-2); толщины стен 300 / 120 мм приняты, межквартирная стена и колонны — по скану, не замерены (К-1); разрешённая мощность 15 кВт принята по типовым ТУ; при объединении двух квартир — переоформление ТУ (К-4); подрайон климата не задан — принят не северный (жилые от 2,5 м) (К-8).

См. лист открытых вопросов (лист 6, записи К-1, К-2, К-4, К-8).

1000 мм · печать 1:1

Изм.	Кол.уч	Лист	№ док.	Подп.	Дата
Разраб.		Кырлан А.С.			04.11.26
Пров.					
ГИП					
Н. контр.					
Утв.					

ГД-2026-009-АИ

Квартира 103 м²

Общая площадь 100,72* м² · * размеры со скана, не замерены (реестр — л. 6, 7, К-1)

Дизайн-проект интерьера

Стадия	Лист	Листов
РП	69	120

Система хранения Пс1

М 1:20

Кырлан Александр Сергеевич


выпуск 04.11.2026 № 20cec94f32 · стр. 77 из 130

Шкаф распашной С2


Спальня 2 (пом. 8) · вид из помещения · размеры в мм, отметки в м

ПРЕДВАРИТЕЛЬНО · не для производства работ · открыто пунктов: 8 (реестр — л. 6, 7)


Вид с фасадами

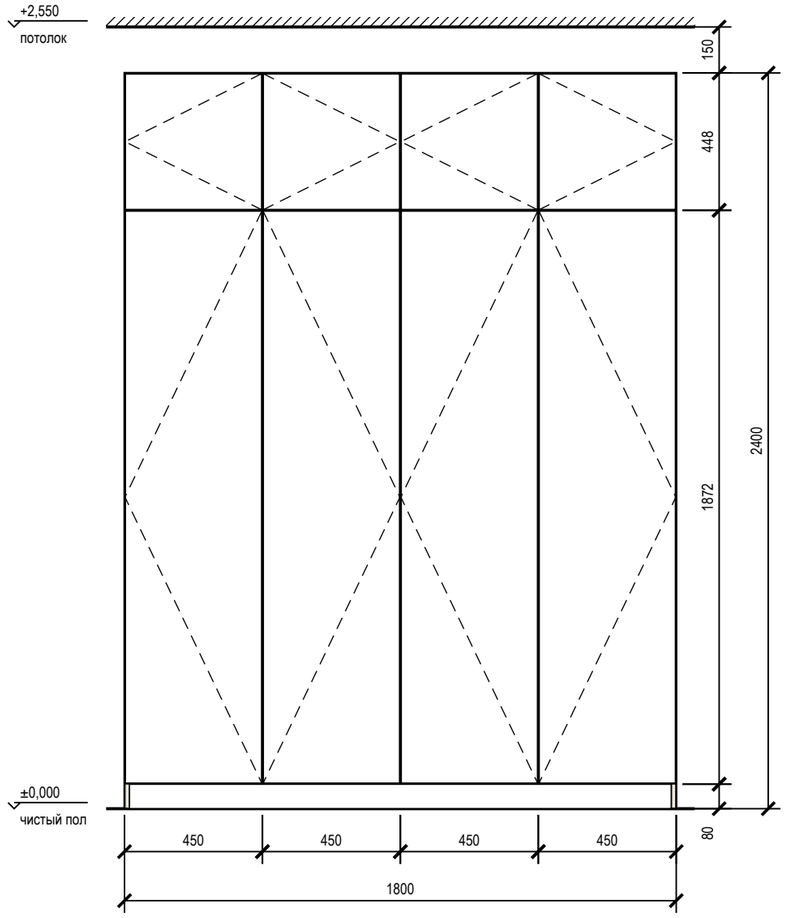


Вид без фасадов

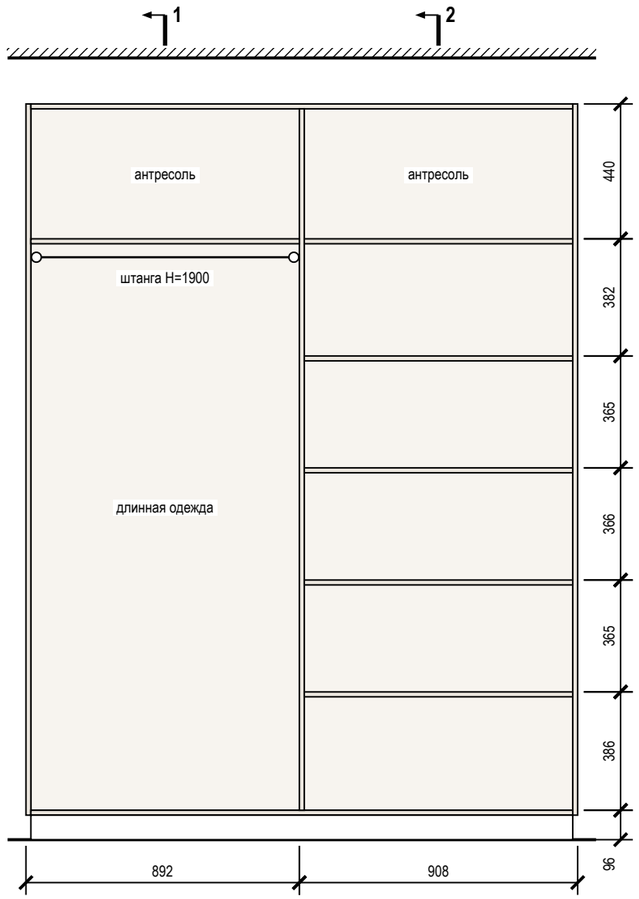

Разрез 1-1

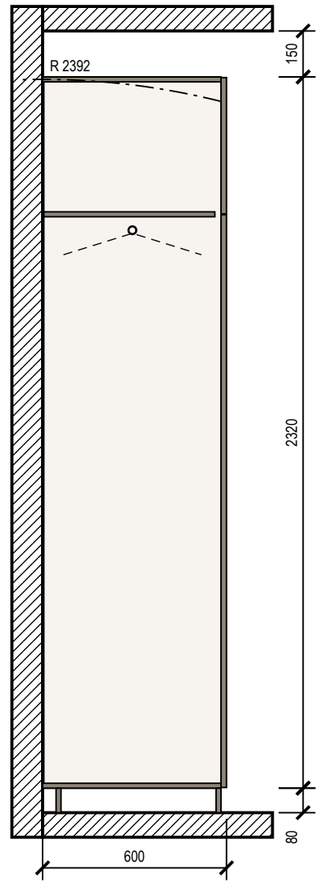

Разрез 2-2

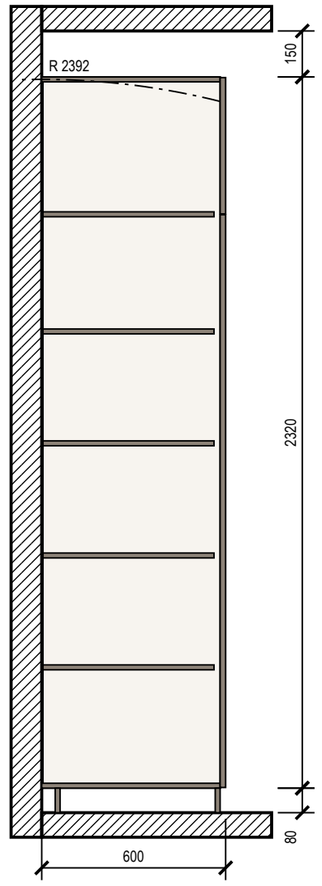

Примечания

1. Размеры — в мм по чистовой отделке; изделие 1800×600×2400 (Ш×Г×В). Перед раскроем — контрольный замер цеха после чистовой отделки стен, пола и потолка.
2. Корпус — ЛДСП 16 мм, задняя стенка ХДФ 4 мм в паз, цоколь 80 мм на регулируемых опорах; фасады накладные — МДФ, шпон ореха 18 мм, масло матовое; цвет — по колерной карте; петли с доводчиком: фасад 1869 мм — 4 петли, фасад 445 мм — 2 петли.
3. Кромка: скрытые торцы 0,4 мм, видимые 2 мм (ПВХ/АБС).
4. Номинальные зазоры: между фасадами 3 мм, фасад — стена и фасад — потолок не менее 3 мм, фасад ящика — стойка 2 мм.
5. Присадка по 32-й системе — выполняет цех.
6. Зазор до потолка 150 мм — закрыть планкой в цвет корпуса при монтаже.
7. Подъём корпуса: диагональ боковины без цоколя $\sqrt{(2320^2 + 582^2)} = 2392$ мм < 2550 мм до потолка — корпус собирается лёжа, поднимается поворотом и ставится на цоколь.
8. Крепление к стене от опрокидывания — уголки 2 шт. к несущему основанию (монтажная схема шкафов).

Условные обозначения

- фасад распашной: линии сходятся к стороне петель
- корпус и полки ЛДСП (вид на стену)
- задняя стенка ХДФ
- деталь в разрезе
- штанга для плечиков (на разрезе — плечики 450 мм)
- траектория угла корпуса при подъёме в проектное положение

Допущения и предложения на листе

Основа листа: размеры сняты со скана обмерного плана KV design (см): часть подписей не читается, помещения выровнены по читаемым размерам; контрольный обмер не выполнен (К-1); высота потолка 2650 мм принята по отметкам обмера (H = 2,50…2,66 м, ригель 2,28 м) — уточнить при обмере (К-2); толщины стен 300 / 120 мм приняты, межквартирная стена и колонны — по скану, не замерены (К-1); разрешённая мощность 15 кВт принята по типовым ТУ; при объединении двух квартир — переоформление ТУ (К-4); подрайон климата не задан — принят не северный (жилые от 2,5 м) (К-8).
См. лист открытых вопросов (лист 6, записи К-1, К-2, К-4, К-8).

1000 мм · печать 1:1

Изм.	Кол.уч	Лист	№ док.	Подп.	Дата
Разраб.		Кырлан А.С.			04.11.26
Пров.					
ГИП					
Н. контр.					
Утв.					

ГД-2026-009-АИ

Квартира 103 м²

Общая площадь 100,72* м² · * размеры со скана, не замерены (реестр — л. 6, 7, К-1)

Дизайн-проект интерьера

Стадия	Лист	Листов
РП	70	120

Шкаф распашной С2

М 1:20

Кырлан Александр Сергеевич


выпуск 04.11.2026 № 20cec94f32 · стр. 78 из 130

Шкаф распашной М4


Спальня мастер (пом. 10) · вид из помещения · размеры в мм, отметки в м

ПРЕДВАРИТЕЛЬНО · не для производства работ · открыто пунктов: 8 (реестр — л. 6, 7)


Вид с фасадами

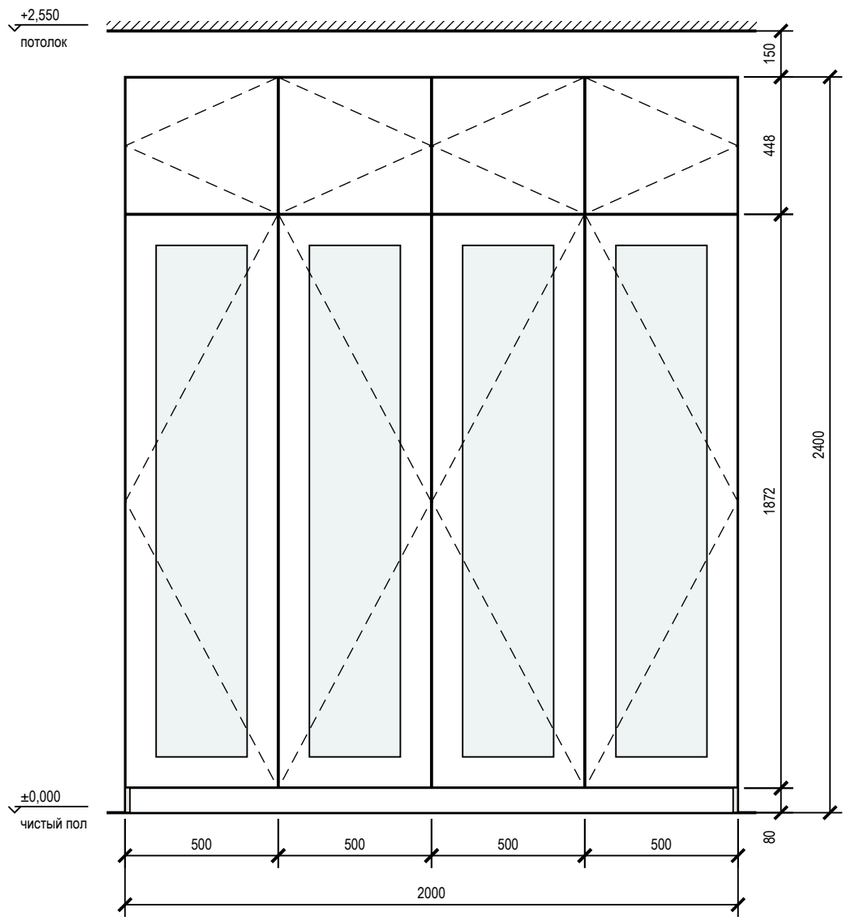


Вид без фасадов

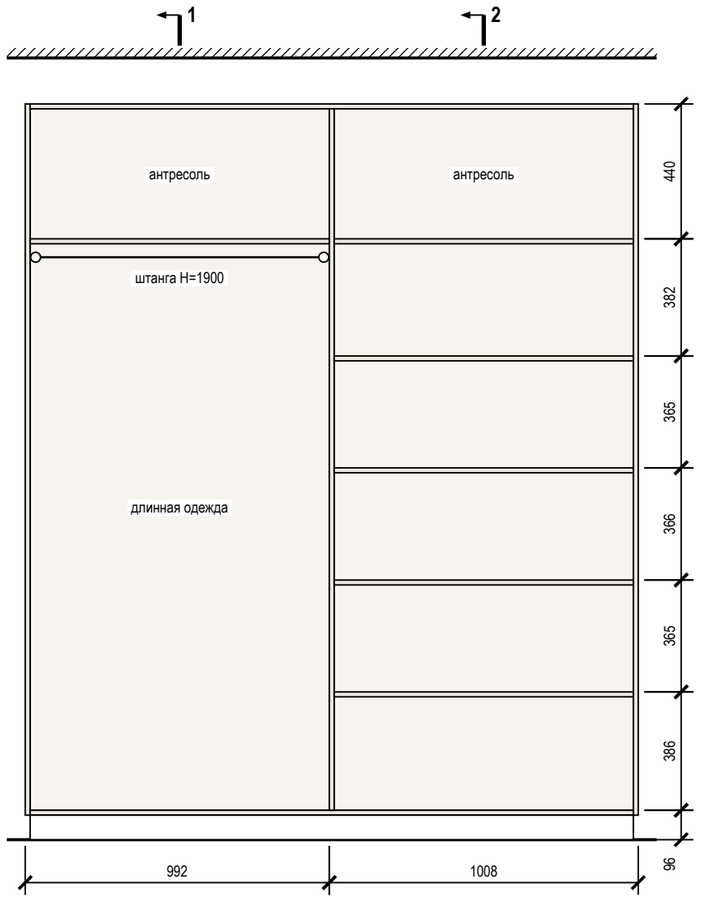

Разрез 1-1

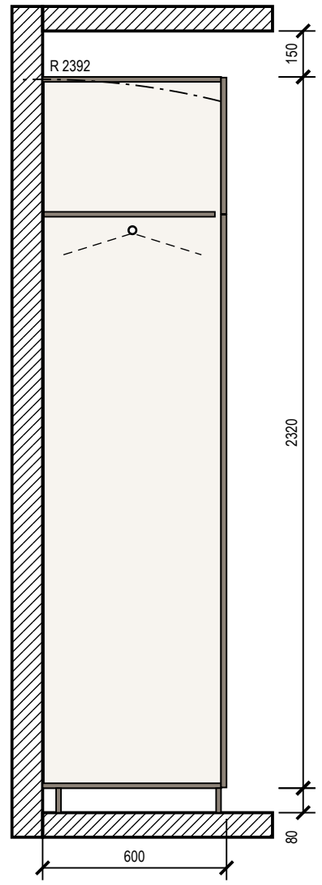

Разрез 2-2

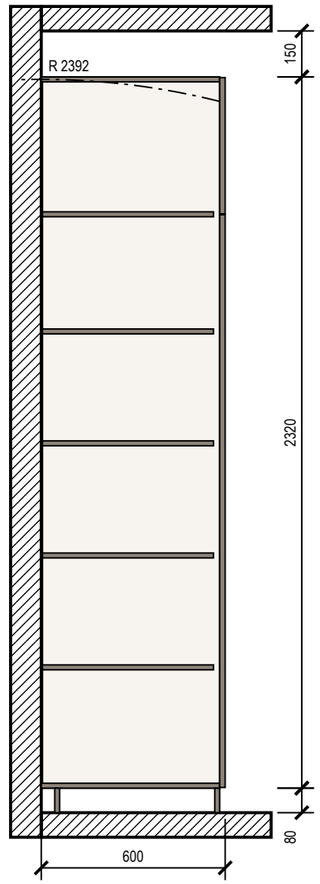

Примечания

1. Размеры — в мм по чистовой отделке; изделие 2000×600×2400 (Ш×Г×В). Перед раскроем — контрольный замер цеха после чистовой отделки стен, пола и потолка.
2. Корпус — ЛДСП 16 мм, задняя стенка ХДФ 4 мм в паз, цоколь 80 мм на регулируемых опорах; фасады накладные — МДФ, шпон ореха 18 мм, масло матовое; вставка — латунь; цвет — по колерной карте; петли с доводчиком: фасад 1869 мм — 4 петли, фасад 445 мм — 2 петли.
3. Кромка: скрытые торцы 0,4 мм, видимые 2 мм (ПВХ/АБС).
4. Номинальные зазоры: между фасадами 3 мм, фасад — стена и фасад — потолок не менее 3 мм, фасад ящика — стойка 2 мм.
5. Присадка по 32-й системе — выполняет цех.
6. Зазор до потолка 150 мм — закрыть планкой в цвет корпуса при монтаже.
7. Подъём корпуса: диагональ боковины без цоколя $\sqrt{(2320^2 + 582^2)} = 2392$ мм < 2550 мм до потолка — корпус собирается лёжа, поднимается поворотом и ставится на цоколь.
8. Крепление к стене от опрокидывания — уголки 2 шт. к несущему основанию (монтажная схема шкафов).

Условные обозначения

- фасад распашной: линии сходятся к стороне петель
- корпус и полки ЛДСП (вид на стену)
- задняя стенка ХДФ
- деталь в разрезе
- штанга для плечиков (на разрезе — плечики 450 мм)
- траектория угла корпуса при подъёме в проектное положение

Допущения и предложения на листе

Основа листа: размеры сняты со скана обмерного плана KV design (см): часть подписей не читается, помещения выровнены по читаемым размерам; контрольный обмер не выполнен (К-1); высота потолка 2650 мм принята по отметкам обмера (H = 2,50…2,66 м, ригель 2,28 м) — уточнить при обмере (К-2); толщины стен 300 / 120 мм приняты, межквартирная стена и колонны — по скану, не замерены (К-1); разрешённая мощность 15 кВт принята по типовым ТУ; при объединении двух квартир — переоформление ТУ (К-4); подрайон климата не задан — принят не северный (жилые от 2,5 м) (К-8).

См. лист открытых вопросов (лист 6, записи К-1, К-2, К-4, К-8).

1000 мм · печать 1:1

Изм.	Кол.уч	Лист	№ док.	Подп.	Дата
Разраб.		Кырлан А.С.			04.11.26
Пров.					
ГИП					
Н. контр.					
Утв.					

ГД-2026-009-АИ

Квартира 103 м²

Общая площадь 100,72* м² · * размеры со скана, не замерены (реестр — л. 6, 7, К-1)

Дизайн-проект интерьера

Стадия	Лист	Листов
РП	71	120

Шкаф распашной М4

М 1:20

Кырлан Александр Сергеевич


выпуск 04.11.2026 № 20cec94f32 · стр. 79 из 130

Кухня (пом. 5). Развёртка гарнитура


Кухня (пом. 5) · стена Б · вид из помещения · размеры в мм, отметки в м

ПРЕДВАРИТЕЛЬНО · не для производства работ · открыто пунктов: 8 (реестр — л. 6, 7)


Вид с фасадами

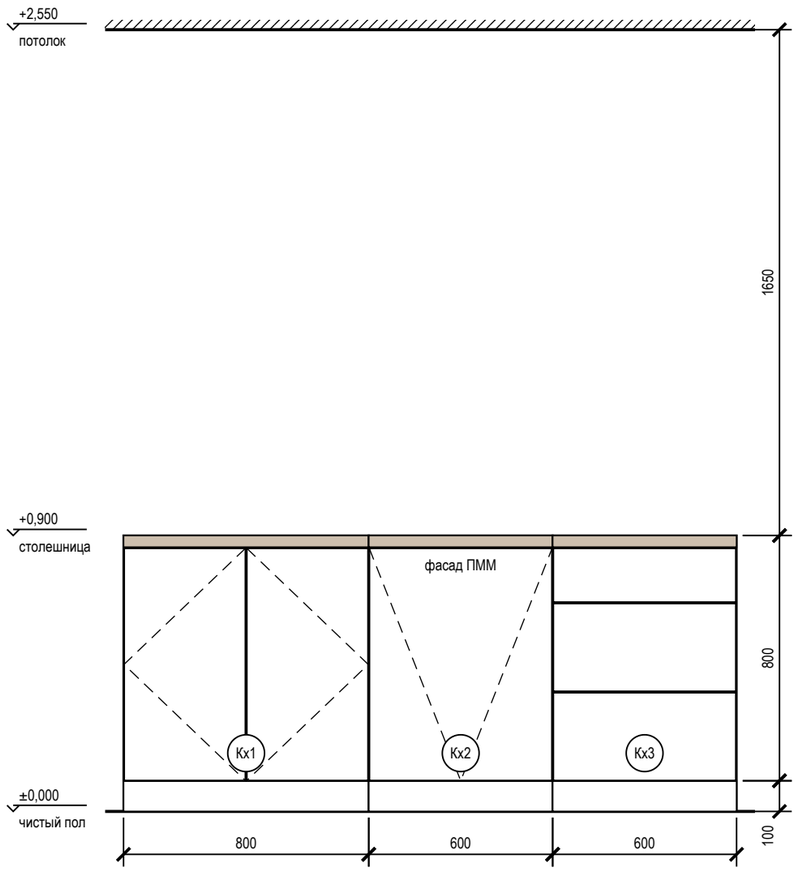

Вид без фасадов (наполнение, выводы)

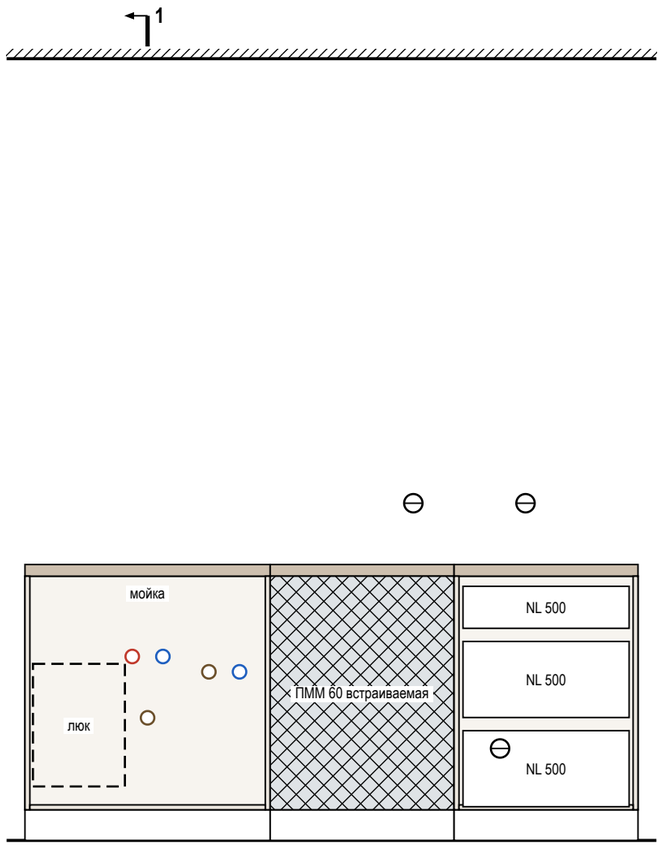

Разрез 1-1

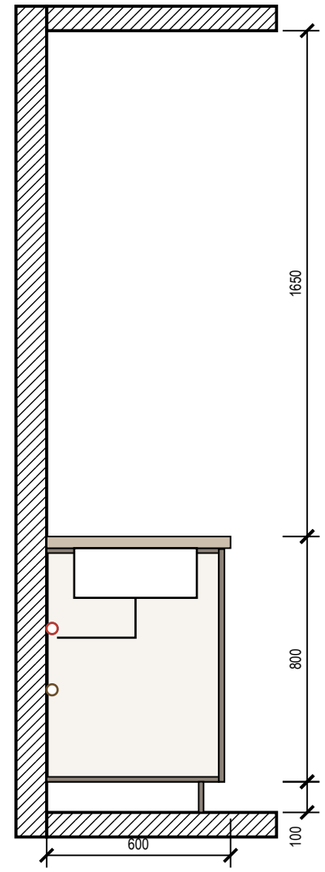

Условные обозначения

- фасад распашной: линии сходятся к стороне петель
- фасад ящика, карго
- встраиваемая техника
- столешница
- доборная планка
- деталь в разрезе
- К1 — марка изделия или модуля (на схеме расположения под ней — лист изделия)
- розетка на стене
- вывод кабеля к технике
- В1 — вывод воды В1 / Т3, канализации К1

Примечания

1. Размеры — в мм по чистовой отделке, вид из помещения; марки — как на плане расстановки. Перед раскроем — контрольный замер цеха после фартука и пола.
2. Корпуса — ЛДСП 16 мм, задняя стенка ХДФ 4 мм; фасады — МДФ, шпон ореха 18 мм, цвет по колерной карте; столешница 38 мм, свес 20 мм; цоколь 100 мм.
3. Кромка: скрытые торцы 0,4 мм, видимые 2 мм. Номинальные зазоры: между фасадами 3 мм, фасад — столешница 3 мм, фасад — стена не менее 3 мм.
4. Ящики полного выдвижения и петли — с доводчиком; присадка по 32-й системе — выполняет цех.
5. Ниши техники — по монтажным схемам выбранных моделей: решётка в цоколе и канал за пеналом холодильника, зазор за духовым шкафом, фасад ПММ на двери машины.
6. Кх1: сервисный люк к стоякам Ст К1-2 (кухня), Ст В1-2, Ст Т3-2 — съёмная панель 300×400 мм в задней стенке на саморезах (по виду без фасадов, штриховой контур «люк»), доступ через фасад модуля; короб стояков за модулем — с ревизией напротив люка (лист ВК).

Допущения и предложения на листе

Основа листа: размеры сняты со скана обмерного плана KV design (см): часть подписей не читается, помещения выровнены по читаемым размерам; контрольный обмер не выполнен (К-1); высота потолка 2650 мм принята по отметкам обмера (Н = 2,50…2,66 м, ригель 2,28 м) — уточнить при обмере (К-2); толщины стен 300 / 120 мм приняты, межквартирная стена и колонны — по скану, не замерены (К-1); разрешённая мощность 15 кВт принята по типовым ТУ; при объединении двух квартир — переоформление ТУ (К-4); подрайон климата не задан — принят не северный (жилые от 2,5 м) (К-8).
См. лист открытых вопросов (лист 6, записи К-1, К-2, К-4, К-8).

1000 мм · печать 1:1

Изм.	Кол.уч	Лист	№ док.	Подп.	Дата
Разраб.		Кырлан А.С.			04.11.26
Пров.					
ГИП					
Н. контр.					
Утв.					

ГД-2026-009-АИ

Квартира 103 м²

Общая площадь 100,72* м² · * размеры со скана, не замерены (реестр — л. 6, 7, К-1)

Дизайн-проект интерьера	Стадия	Лист	Листов
	РП	72	120

Кухня (пом. 5). Развёртка гарнитура

М 1:20

Кырлан Александр Сергеевич


выпуск 04.11.2026 № 20cec94f32 · стр. 80 из 130

Кухня (пом. 5). Монтажная схема


Кухня (пом. 5) · стена Б · размеры в мм от чистых поверхностей, высоты — от чистого пола

ПРЕДВАРИТЕЛЬНО · не для производства работ · открыто пунктов: 8 (реестр — л. 6, 7)

Привязка выводов и крепление модулей

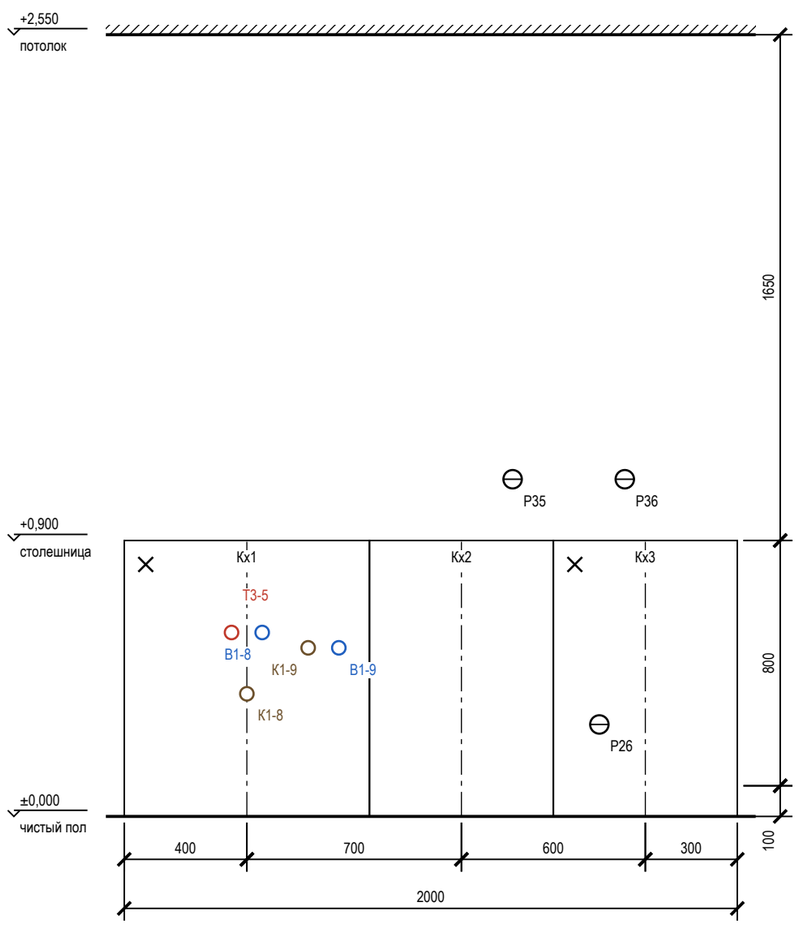

План столешницы

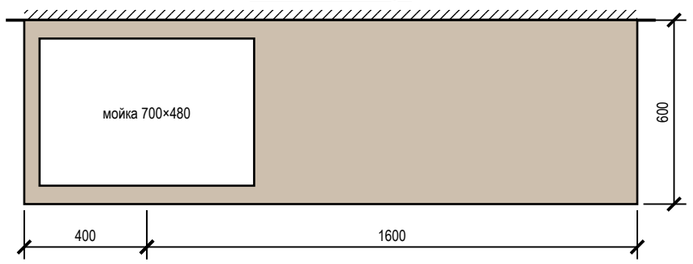

Привязка выводов к осям модулей

Код	Назначение	Модуль	От оси, мм	Н, мм	Размещение
Т3-5	Т3 — межос. 100	Кх1	−50	600	в модуле мойки
К1-8	К1 Ø50 — мойка	Кх1	0	400	в модуле мойки
В1-8	В1 — межос. 100	Кх1	+50	600	в модуле мойки
К1-9	К1 Ø40 — слив ПММ в шкафу мойки	Кх1	+200	550	в модуле мойки
В1-9	В1 — кран ПММ в шкафу мойки	Кх1	+300	550	в модуле мойки
Р35	розетка ×2 — фартук	Кх2	+167	1100	над столешницей (фартук)
Р26	розетка — посудомоечная машина — в соседнем модуле, за ящиком	Кх3	−150	300	в соседнем модуле, за ящиком
Р36	розетка ×2 — фартук	Кх3	−67	1100	над столешницей (фартук)

Зазоры под отделку

Поверхность	Отделка	Зазор, мм	Учесть
фартук	керамогранит	10	от чернового основания до корпуса навесных и столешницы
стены	окраска	5	под штукатурку и шпаклёвку за пеналом
пол	инженерная доска		цоколь — после укладки пола, опоры ±20 мм

Условные обозначения

- нижний модуль, пенал (контур)
- ось модуля (от неё — привязка вывода)
- анкер / уголок крепления к стене
- розетка на стене
- вывод кабеля к технике
- В1 — вывод воды В1 / Т3, канализации К1

Допущения и предложения на листе

Основа листа: размеры сняты со скана обмерного плана KV design (см): часть подписей не читается, помещения выровнены по читаемым размерам; контрольный обмер не выполнен (К-1); высота потолка 2650 мм принята по отметкам обмера (Н = 2,50…2,66 м, ригель 2,28 м) — уточнить при обмере (К-2); толщины стен 300 / 120 мм приняты, межквартирная стена и колонны — по скану, не замерены (К-1); разрешённая мощность 15 кВт принята по типовым ТУ; при объединении двух квартир — переоформление ТУ (К-4); подрайон климата не задан — принят не северный (жилые от 2,5 м) (К-8).

См. лист открытых вопросов (лист 6, записи К-1, К-2, К-4, К-8).

Примечания

1. Выводы — по проекту электрики и ВК; привязка по горизонтали — от оси модуля (плюс — вправо по виду), по высоте — от чистого пола до оси вывода.
2. Пенал — уголки к стене 2 шт. сверху; нижние модули — стяжками между собой и уголком к стене; ряд выставить по уровню опорами цоколя.
3. Розетки над столешницей — не ниже 150 мм над ней и не за корпусом техники; розетка за ПММ, духовым шкафом и холодильником — только в соседнем модуле или в зоне цоколя с доступом.
4. Столешница — вырезы по шаблонам выбранных моделей мойки и варочной панели; торцы у стены — герметик, пристеночный плинтус.

1000 мм · печать 1:1

Изм.	Кол.уч	Лист	№ док.	Подп.	Дата
Разраб.		Кырлан А.С.			04.11.26
Пров.					
ГИП					
Н. контр.					
Утв.					

ГД-2026-009-АИ

Квартира 103 м²

Общая площадь 100,72* м² · * размеры со скана, не замерены (реестр — л. 6, 7, К-1)

Дизайн-проект интерьера

Стадия	Лист	Листов
РП	73	120

Кухня (пом. 5). Монтажная схема

М 1:20

Кырлан Александр Сергеевич


выпуск 04.11.2026 № 20cec94f32 · стр. 81 из 130

Кухня (пом. 5). Развёртка гарнитура


Кухня (пом. 5) · стена В · вид из помещения · размеры в мм, отметки в м

ПРЕДВАРИТЕЛЬНО · не для производства работ · открыто пунктов: 8 (реестр — л. 6, 7)


Вид с фасадами

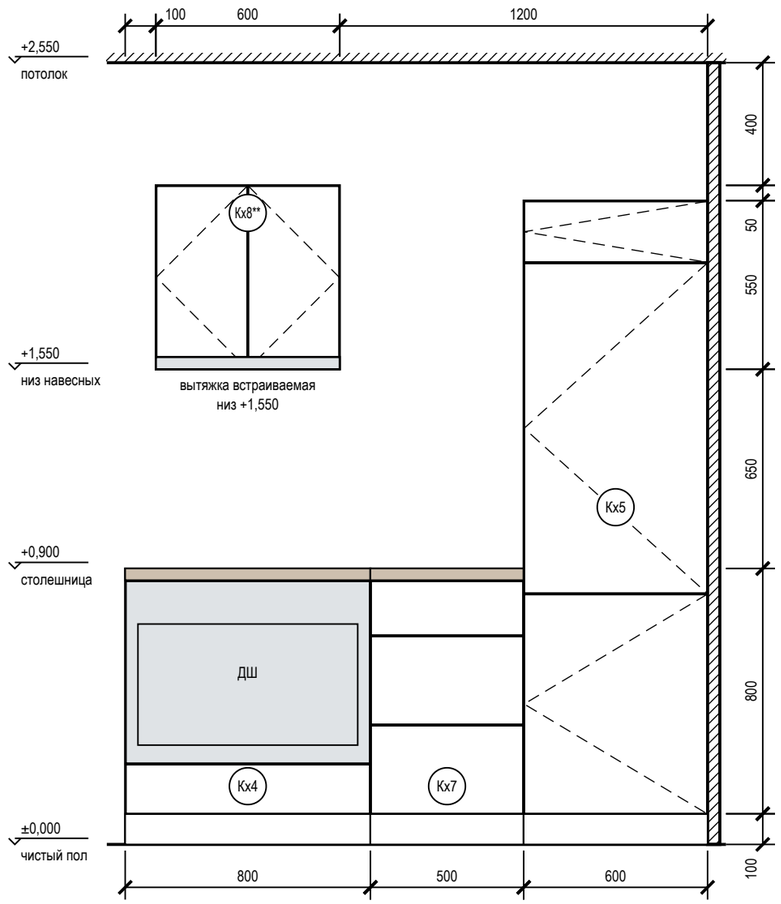


Вид без фасадов (наполнение, выводы)

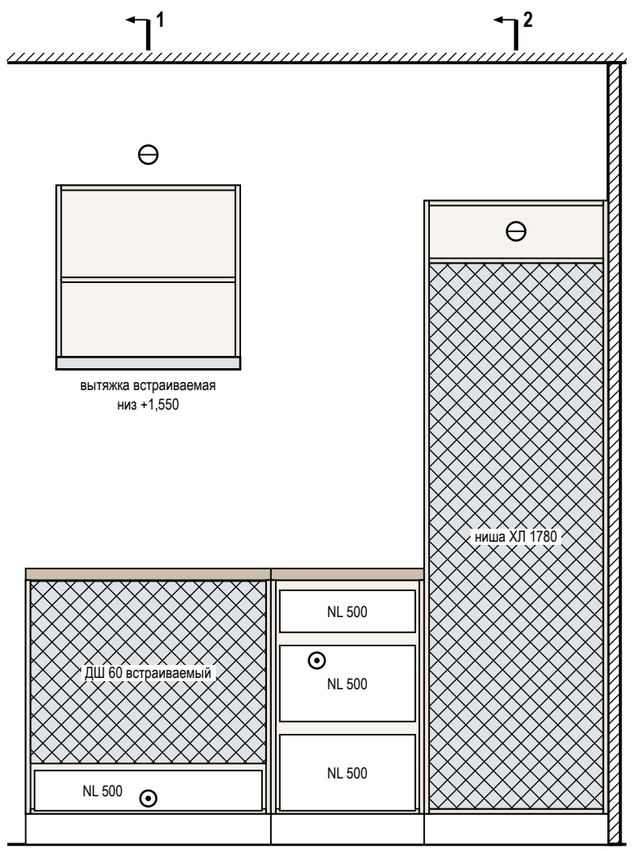

Разрез 1-1

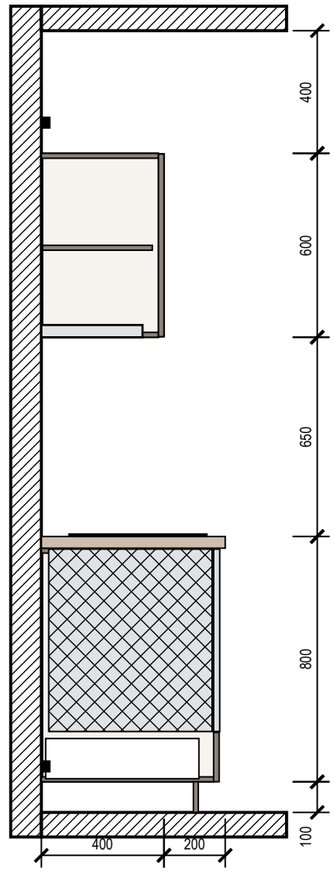

Разрез 2-2

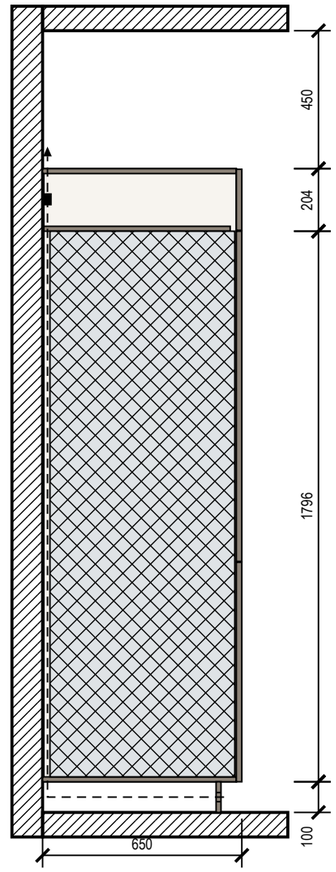

Условные обозначения

- фасад распашной: линии сходятся к стороне петель
- фасад ящика, карго
- встраиваемая техника
- столешница
- доборная планка
- деталь в разрезе
- К1 — марка изделия или модуля (на схеме расположения под ней — лист изделия)
- розетка на стене
- вывод кабеля к технике
- В1 — вывод воды В1 / Т3, канализации К1

1000 мм · печать 1:1

Примечания

1. Размеры — в мм по чистовой отделке, вид из помещения; марки — как на плане расстановки. Перед раскроем — контрольный замер цеха после фартука и пола.
2. Корпуса — ЛДСП 16 мм, задняя стенка ХДФ 4 мм; фасады — МДФ, эмаль матовая 18 мм, цвет по колерной карте; столешница 38 мм, свес 20 мм; цоколь 100 мм.
3. Кромка: скрытые торцы 0,4 мм, видимые 2 мм. Номинальные зазоры: между фасадами 3 мм, фасад — столешница 3 мм, фасад — стена не менее 3 мм.
4. Ящики полного выдвижения и петли — с доводчиком; присадка по 32-й системе — выполняет цех.
5. Вытяжка встраивается в дно навесного модуля Кх8** над варочной: её низ на 1550 мм от пола, 650 мм над панелью (не меньше 650 мм).
6. Ниши техники (холодильник — ориентир 1780 мм) — по монтажным схемам выбранных моделей: решётка в цоколе и канал за пеналом холодильника, зазор за духовым шкафом, фасад ПММ на двери машины.

Допущения и предложения на листе

Основа листа: размеры сняты со скана обмерного плана KV design (см): часть подписей не читается, помещения выровнены по читаемым размерам; контрольный обмер не выполнен (К-1); высота потолка 2650 мм принята по отметкам обмера (Н = 2,50…2,66 м, ригель 2,28 м) — уточнить при обмере (К-2); толщины стен 300 / 120 мм приняты, межквартирная стена и колонны — по скану, не замерены (К-1); разрешённая мощность 15 кВт принята по типовым ТУ; при объединении двух квартир — переоформление ТУ (К-4); подрайон климата не задан — принят не северный (жилые от 2,5 м) (К-8).
Знак «**» — предложение проектировщика, заказчиком не утверждено (согласовать с заказчиком): Кх8 — над индукционной панелью Кх4 нужна вытяжка: в составе кухни её не было, розетка вытяжки образца висела без потребителя.
См. лист открытых вопросов (лист 6, записи К-1, К-2, К-4, К-8).

Изм.	Кол.уч	Лист	№ док.	Подп.	Дата
Разраб.		Кырлан А.С.			04.11.26
Пров.					
ГИП					
Н. контр.					
Утв.					

ГД-2026-009-АИ

Квартира 103 м²

Общая площадь 100,72* м² · * размеры со скана, не замерены (реестр — л. 6, 7, К-1)

Дизайн-проект интерьера	Стадия	Лист	Листов
	РП	74	120

Кухня (пом. 5). Развёртка гарнитура

М 1:20


Кырлан Александр Сергеевич

выпуск 04.11.2026 № 20cec94f32 · стр. 82 из 130


Кухня (пом. 5). Монтажная схема

Кухня (пом. 5) · стена В · размеры в мм от чистых поверхностей, высоты — от чистого пола

Привязка выводов и крепление модулей

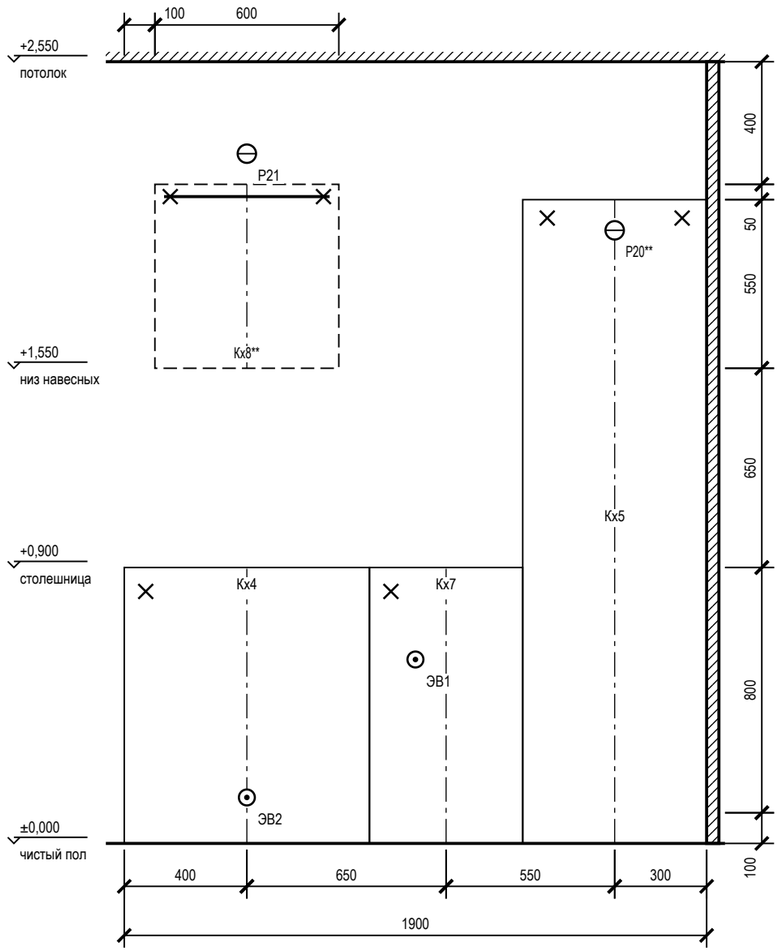

План столешницы

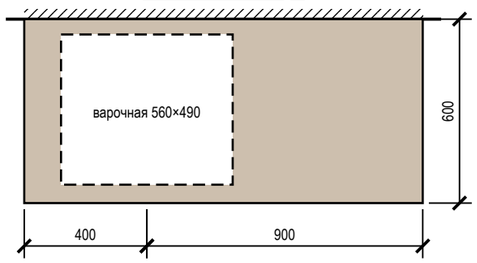

Привязка выводов к осям модулей

Код	Назначение	Модуль	От оси, мм	Н, мм	Размещение
ЭВ2	вывод кабеля — духовой шкаф — в цоколе	Кх4	0	150	под духовым шкафом, доступ через ящик
P21	розетка — вытяжка — над корпусом	Кх8**	0	2250	в навесном модуле
ЭВ1	вывод кабеля — варочная панель — в соседнем модуле, за ящиком	Кх7	−100	600	в соседнем модуле, за ящиком
P20**	розетка — холодильник — над нишей, съёмная панель	Кх5	0	2000	над нишей холодильника, съёмная панель

Зазоры под отделку

Поверхность	Отделка	Зазор, мм	Учесть
фартук	керамогранит	10	от чернового основания до корпуса навесных и столешницы
стены	окраска	5	под штукатурку и шпаклёвку за пеналом
пол	инженерная доска		цоколь — после укладки пола, опоры ±20 мм

Условные обозначения

- нижний модуль, пенал (контур)
- невидимый контур: навесной модуль, корпус под столешницей
- ось модуля (от неё — привязка вывода)
- анкер / уголок крепления к стене
- розетка на стене
- вывод кабеля к технике
- B1 — вывод воды В1 / Т3, канализации К1

Допущения и предложения на листе

Основа листа: размеры сняты со скана обмерного плана KV design (см): часть подписей не читается, помещения выровнены по читаемым размерам; контрольный обмер не выполнен (К-1); высота потолка 2650 мм принята по отметкам обмера (Н = 2,50…2,66 м, ригель 2,28 м) — уточнить при обмере (К-2); толщины стен 300 / 120 мм приняты, межквартирная стена и колонны — по скану, не замерены (К-1); разрешённая мощность 15 кВт принята по типовым ТУ; при объединении двух квартир — переоформление ТУ (К-4); подрайон климата не задан — принят не северный (жилые от 2,5 м) (К-8).

Знак «**» — предложение проектировщика, заказчиком не утверждено (согласовать с заказчиком): Кх8 — над индукционной панелью Кх4 нужна вытяжка: в составе кухни её не было, розетка вытяжки образца висела без потребителя; Р20 — высота 2000 мм выше нормы 1 м (ПУЭ 6.6.30) по назначению: розетка встроенного прибора — в колонне Кх5 над нишей, в антресоли за съёмной панелью.

См. лист открытых вопросов (лист 6, записи К-1, К-2, К-4, К-8).

Примечания

1. Выводы — по проекту электрики и ВК; привязка по горизонтали — от оси модуля (плюс — вправо по виду), по высоте — от чистого пола до оси вывода.
2. Пенал — уголки к стене 2 шт. сверху; нижние модули — стяжками между собой и уголком к стене; ряд выставить по уровню опорами цоколя.
3. Розетки над столешницей — не ниже 150 мм над ней и не за корпусом техники; розетка за ПММ, духовым шкафом и холодильником — только в соседнем модуле или в зоне цоколя с доступом.
4. Столешница — вырезы по шаблонам выбранных моделей мойки и варочной панели; торцы у стены — герметик, пристеночный плинтус.

1000 мм · печать 1:1

Изм.	Кол.уч	Лист	№ док.	Подп.	Дата
Разраб.		Кырлан А.С.			04.11.26
Пров.					
ГИП					
Н. контр.					
Утв.					

ГД-2026-009-АИ

Квартира 103 м²

Общая площадь 100,72* м² · * размеры со скана, не замерены (реестр — л. 6, 7, К-1)

Дизайн-проект интерьера

Стадия	Лист	Листов
РП	75	120

Кухня (пом. 5). Монтажная схема

М 1:20

Кырлан Александр Сергеевич


выпуск 04.11.2026 № 20cec94f32 · стр. 83 из 130

Шкафы. Монтажная схема


крепление к стене, установочные размеры, зазоры под отделку · размеры в мм

ПРЕДВАРИТЕЛЬНО · не для производства работ · открыто пунктов: 8 (реестр — л. 6, 7)


Система хранения Кл1 (пом. 2)

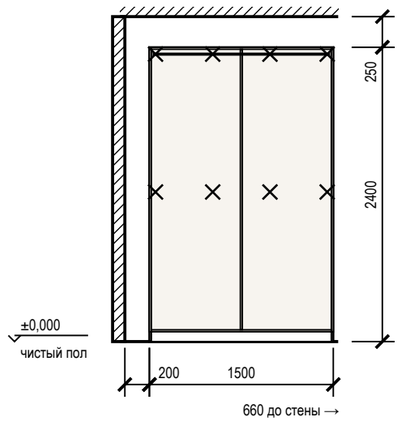


Шкаф-купе П1 (пом. 4)

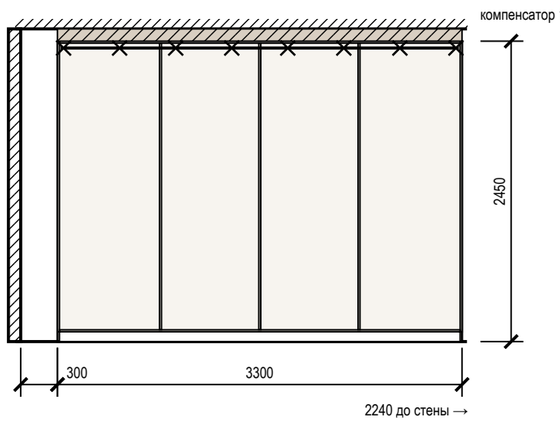


Система хранения Пс1 пом. 7

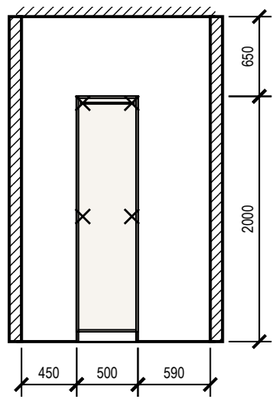

Шкаф распашной С2 (пом. 8)

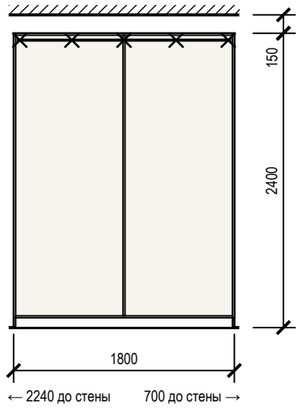

Шкаф распашной М4 (пом. 10)

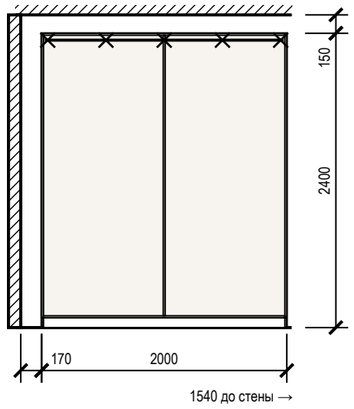

Крепление и зазоры под отделку

Марка	Помещение, стена	Основание	Отделка стены	Зазор, мм	Крепёж по планке	От опрокидывания
Кл1	Кладовая (2), стена Б	по основанию — см. таблицу крепежа	окраска	5	анкер 8 шт. (2 ряда)	уголки 2 шт.
П1	Прихожая-холл (4), стена А	по основанию — см. таблицу крепежа	окраска	5	анкер 8 шт., шаг 457	уголки 2 шт.
Пс1	Постирочная (7), стена Б	по основанию — см. таблицу крепежа	окраска	5	анкер 4 шт. (2 ряда)	уголки 2 шт.
С2	Спальня 2 (8), стена А	по основанию — см. таблицу крепежа	окраска	5	анкер 5 шт., шаг 425	уголки 2 шт.
М4	Спальня мастер (10), стена Г	по основанию — см. таблицу крепежа	окраска	5	анкер 5 шт., шаг 475	уголки 2 шт.

Крепёж по основанию стены

Основание стены	Крепёж
бетон, ж/б	анкер-шуруп 7,5×72 или дюбель 8×60 с шурупом 5×70
кирпич полнотелый	дюбель 8×80 с шурупом 5×90
газобетон, пазогребень	дюбель для газобетона 10×100 или химический анкер
гипсокартон	закладная до обшивки (брус 40×80 или фанера 18 мм), саморез в закладную

Условные обозначения

- анкер / уголок крепления к стене
- корпус и полки ЛДСП (вид на стену)
- компенсатор — короб до потолка

Примечания

1. Установочные размеры — от чистого пола и чистых стен; перед установкой контрольный замер после отделки.
2. Порядок: корпус выставить по уровню опорами цоколя → закрепить к стене по задней планке → навесить двери и фасады, отрегулировать зазоры → подогнать и закрепить компенсатор.
3. Анкеры — с шагом не более 500 мм, не ближе 50 мм от края планки; на ГКЛ только в закладную, установленную до обшивки.
4. Скрытые коммуникации под анкеры проверить детектором; трассы электрики по плану розеток.

Допущения и предложения на листе

Основа листа: размеры сняты со скана обмерного плана KV design (см): часть подписей не читается, помещения выровнены по читаемым размерам; контрольный обмер не выполнен (К-1); высота потолка 2650 мм принята по отметкам обмера (Н = 2,50…2,66 м, ригель 2,28 м) — уточнить при обмере (К-2); толщины стен 300 / 120 мм приняты, межквартирная стена и колонны — по скану, не замерены (К-1); разрешённая мощность 15 кВт принята по типовым ТУ; при объединении двух квартир — переоформление ТУ (К-4); подрайон климата не задан — принят не северный (жилые от 2,5 м) (К-8).
См. лист открытых вопросов (лист 6, записи К-1, К-2, К-4, К-8).

1000 мм · печать 1:1

Изм.	Кол.уч	Лист	№ док.	Подп.	Дата
Разраб.		Кырлан А.С.			04.11.26
Пров.					
ГИП					
Н. контр.					
Утв.					

ГД-2026-009-АИ

Квартира 103 м²

Общая площадь 100,72* м² · * размеры со скана, не замерены (реестр — л. 6, 7, К-1)

Дизайн-проект интерьера

Стадия	Лист	Листов
РП	76	120

Шкафы. Монтажная схема

М 1:50

Кырлан Александр Сергеевич

Ведомости изделий, техники и фурнитуры

встроенная мебель и кухонный гарнитур · размеры в мм

Ведомость изделий

Марка	Наименование	Пом.	Ш×Г×В, мм	Корпус	Фасад	Кромка, мм	Кол.
Кл1	Система хранения	2	1500×400×2400	ЛДСП декор «орех» 16	без фасадов	0,4 / 2	1
П1	Шкаф-купе	4	3300×600×2450	ЛДСП 16	МДФ, шпон ореха 10 мм, масло матовое в профиле: латунь	0,4 / 2	1
Пс1	Система хранения	7	500×300×2000	ЛДСП 16	без фасадов	0,4 / 2	1
С2	Шкаф распашной	8	1800×600×2400	ЛДСП 16	МДФ, шпон ореха 18 мм, масло матовое	0,4 / 2	1
М4	Шкаф распашной	10	2000×600×2400	ЛДСП 16	МДФ, шпон ореха 18 мм, масло матовое; вставка — латунь	0,4 / 2	1
Кх1	Модуль нижний: мойка	5	800×600×900	ЛДСП 16	МДФ, шпон ореха 18 мм, масло матовое	0,4 / 2	1
Кх2	Модуль под ПММ 60: без корпуса, фасад на дверь машины	5	600×600×900	без корпуса	МДФ 18 мм, эмаль матовая — на дверь машины (навеска из её комплекта), цоколь		1
Кх3	Модуль нижний: ящики	5	600×600×900	ЛДСП 16	МДФ 18 мм, эмаль матовая	0,4 / 2	1
Кх4	Модуль нижний: духовой шкаф, варочная	5	800×600×900	ЛДСП 16	МДФ 18 мм, эмаль матовая	0,4 / 2	1
Кх8**	Модуль навесной: полки	5	600×400×600	ЛДСП 16	МДФ 18 мм, эмаль матовая	0,4 / 2	1
Кх7	Модуль нижний: ящики	5	500×600×900	ЛДСП 16	МДФ 18 мм, эмаль матовая	0,4 / 2	1
Кх5	Пенал: холодильник встр.	5	600×650×2100	ЛДСП 16	МДФ эмаль 18 мм, матовая; цвет — тил	0,4 / 2	1

Ведомость встраиваемой техники

Поз.	Прибор	Ниша, вырез, мм	Вентиляция	Питание	Схема
Кх1	Мойка врезная / подстольная с сифоном	вырез по шаблону, ориентир 700 × 480		смеситель — выводы ВК	по модели
Кх2	Посудомоечная машина встраиваемая, 60 см	ниша 600 × 862 (от пола до низа столешницы)	зазор в цоколе, по схеме	Р26: Кх3, Н=300 — в соседнем модуле, за ящиком	по модели
Кх4	Духовой шкаф встраиваемый, 60 см	ниша 560 × 600, глубина ≥ 550	зазор за шкафом, вырез в задней стенке	ЭВ2: Кх4, Н=150 — под духовым шкафом, доступ через ящик	по модели
Кх4	Варочная панель индукционная, 60 см	вырез в столешнице 560 × 490		ЭВ1: Кх7, Н=600 — в соседнем модуле, за ящиком	по модели
Кх5	Холодильник встраиваемый, ниша 1780	ниша 1780 × 560 × 550	решётка в цоколе, канал за корпусом, выход сверху	Р20**: Кх5, Н=2000 — над нишей холодильника, съёмная панель	по модели
Кх8**	Вытяжка встраиваемая в навесной модуль, 60 см	низ ≥ 650 над панелью	воздуховод к вентканалу, короб до потолка	Р21: Кх8**, Н=2250 — в навесном модуле	по модели

Ведомость фурнитуры

№	Фурнитура	Тип, размер	Изделия	Кол.
1	Полкодержатель с фиксацией	ø5 мм	Кл1, П1, Пс1, С2, М4, Кх8**, Кх5	136
2	Штанга выдвижная торцевая	L по глубине	Кл1	1
3	Опора регулируемая с цоколем на клипсах	ход 20 мм	Кл1, П1, Пс1, С2, М4	38
4	Анкер по основанию стены	по таблице крепежа	Кл1, П1, Пс1, С2, М4, Кх8**	32
5	Уголок крепления к стене от опрокидывания	стальной	Кл1, П1, Пс1, С2, М4, Кх5	12
6	Система дверей купе: профиль, направляющие, ролики	на 4 двери	П1	1
7	Ручка-профиль вертикальная	в цвет профиля	П1	4
8	Штанга овальная 30×15, L = 817	+ 2 держателя	П1	1
9	Полка для обуви выдвижная наклонная	ширина 817	П1	3
10	Полка для обуви выдвижная наклонная	ширина 794	П1	3
11	Штанга овальная 30×15, L = 794	+ 2 держателя	П1	1
12	Петля накладная 110° с доводчиком	чашка 35 мм	С2, М4, Кх1, Кх8**, Кх5	63
13	Штанга овальная 30×15, L = 876	+ 2 держателя	С2	1
14	Штанга овальная 30×15, L = 976	+ 2 держателя	М4	1
15	Ручка-профиль	латунь матовая	Кх1, Кх2, Кх3, Кх4, Кх8**, Кх7, Кх5	15
16	Опора кухонная регулируемая 100–120 мм	+ клипса цоколя	Кх1, Кх3, Кх4, Кх7, Кх5	24
17	Комплект навески фасада ПММ	из поставки машины	Кх2	1
18	Направляющие полного выдвижения с доводчиком NL 500	пара	Кх3, Кх4, Кх7	7
19	Навес регулируемый для навесного шкафа	пара на секцию	Кх8**	1
20	Шина монтажная	L = 540	Кх8**	1

Примечания

1. Модели техники выбирает заказчик до изготовления мебели; ниши, вырезы и вентиляция — по монтажной схеме выбранной модели (условие гарантии), её номер вносится в ведомость.
2. Количество фурнитуры — по чертежам изделий; запас крепежа 5 %. Аналоги — по характеристикам (доводчик, нагрузка, ход).
3. Цвет корпусов, фасадов и профилей — по колерной карте проекта. Кромка — скрытые / видимые торцы, мм.

Допущения и предложения на листе

Основа листа: размеры сняты со скана обмерного плана KV design (см): часть подписей не читается, помещения выровнены по читаемым размерам; контрольный обмер не выполнен (К-1); высота потолка 2650 мм принята по отметкам обмера (Н = 2,50…2,66 м, ригель 2,28 м) — уточнить при обмере (К-2); толщины стен 300 / 120 мм приняты, межквартирная стена и колонны — по скану, не замерены (К-1); разрешённая мощность 15 кВт принята по типовым ТУ; при объединении двух квартир — переоформление ТУ (К-4); подрайон климата не задан — принят не северный (жилые от 2,5 м) (К-8).

Знак «**» — предложение проектировщика, заказчиком не утверждено (согласовать с заказчиком): Кх8 — над индукционной панелью Кх4 нужна вытяжка: в составе кухни её не было, розетка вытяжки образца висела без потребителя; Р20 — высота 2000 мм выше нормы 1 м (ПУЭ 6.6.30) по назначению: розетка встроенного прибора — в колонне Кх5 над нишей, в антресоли за съёмной панелью.

См. лист открытых вопросов (лист 6, записи К-1, К-2, К-4, К-8).

Изм.	Кол.уч	Лист	№ док.	Подп.	Дата
Разраб.		Кырлан А.С.			04.11.26
Пров.					
ГИП					
Н. контр.					
Утв.					

ГД-2026-009-АИ

Квартира 103 м²

Общая площадь 100,72* м² · * размеры со скана, не замерены (реестр — л. 6, 7, К-1)

Дизайн-проект интерьера	Стадия	Лист	Листов
	РП	77	120

Ведомости изделий, техники и фурнитуры

М б/м

Кырлан Александр Сергеевич

09

Развёртки и узлы



Кырлан Александр Сергеевич

выпуск 04.11.2026 № 20cec94f32 · стр. 86 из 130

Реестр марок отделки и позиций альбома

Реестр марок отделки (О ↔ позиции колерной карты) и марки позиций по видам

Реестр марок отделки альбома

Марка	Поверхность	Материал, изделие	Цвет, код	Помещения	Колер. карта
О1	стены	окраска, Farrow & Ball Modern Emulsion, матовая, подготовка Q3	Farrow & Ball No. 291 «School House White тёплый меловой белый»	1, 3, 4, 5, 8, 9, 10	К1
О2	акцентная стена	окраска, Farrow & Ball Modern Emulsion, матовая, подготовка Q3	Farrow & Ball No. 289 «Inchyra Blue — тёмный сине-серый»	1, 8, 10	К2
О3	плинтус	плинтус МДФ, h 83 мм, Ultrawood Base 5340, ЛДФ под окраску, 83×15 мм, 2440 мм (арт. LDF-BASE-5340)	Farrow & Ball No. 291 «School House White тёплый меловой белый»	1, 3, 4, 5, 8, 9, 10	К4, К8
О4	потолок	окраска, Tikkurila Anti-Reflex 2, глубокоматовая, подготовка Q3	NCS S 0502-Y «Белый с лёгкой желтизной»	1, 2, 4, 7, 8, 9, 10	К3
О5	пол	инженерная доска, Coswick Вековые традиции, 2100×127 мм, 1167-4250		1, 2, 3, 5, 7, 8, 9, 10	КМ1
О6	стены	окраска, Tikkurila Harmony, матовая, подготовка Q3	NCS S 0502-Y «Белый с лёгкой желтизной»	2, 7	К5
О7	плинтус	плинтус МДФ, h 83 мм, Ultrawood Base 5340, ЛДФ под окраску, 83×15 мм, 2440 мм (арт. LDF-BASE-5340)	NCS S 0502-Y «Белый с лёгкой желтизной»	2, 7	К6
О8	акцентная стена	окраска, Farrow & Ball Modern Emulsion, аналог: интерьерная краска Farrow & Ball Modern Emulsion в цвете веера No. 255, матовая, матовая, подготовка К3	Farrow & Ball No. 255 «Tanner's Brown тёмный шоколад»	3	К7
О9	потолок	окраска, Farrow & Ball Modern Emulsion, матовая, подготовка Q3	Farrow & Ball No. 291 «School House White тёплый меловой белый»	3, 5	К1
О10	пол	керамогранит, Atlas Concorde Marvel Travertine, 600×1200×9 мм, A8UZ, затирка CG2WA	Atlas Concorde A8UZ «Marvel Travertine»	4	КМ2
О11	фартук	керамогранит, аналог: керамогранит матовый, тон F497, затирка CG2WA	#F1F1EC «тон Paper F497»	5	КМ3
О12	стены	облицовка плиткой, Atlas Concorde Marvel Travertine, 600×1200×9 мм, A8UZ, затирка CG2WA	Atlas Concorde A8UZ «Marvel Travertine»	6, 11	КМ4
О13	потолок	окраска, Tikkurila Luja 7, матовая, подготовка Q3	NCS S 0502-Y «Белый с лёгкой желтизной»	6, 11	К9
О14	пол	керамогранит, 600×600×9 мм, Atlas Concorde Marvel Travertine Sand Cross 60×60 Matte Sensitech, арт. AFUL (той же коллекции, что стены A8UZ; тон сверить по образцу), затирка CG2WA		6, 11	КМ5

Марки позиций альбома по видам

Префикс	Что обозначает, позиции	Листы
Д	двери: Д-1–Д-9	14–17
ПР	проёмы без полотна (порталы): ПР-1	14–17
ОК	окна: ОК-1–ОК-7	14–17
Б, Г, Кл, Кх, М, П, Пс, С	мебель и оборудование: Б1–Б4, Г1–Г6, Кл1, Кх1–Кх7, Кх8**, М1–М6, П1–П3, Пс1, С1–С3	18–22
Пм, См, Сн	сантехнические приборы: Пм1, См1–См4, Сн1–Сн4	33–42

Допущения и предложения на листе. Знак «*» принято (замерить). Знак «**» предложено (согласовать): плинтус пом. 1–5, 7–10, акцент пом. 3, фартук пом. 5, пол пом. 6, 11. См. лист открытых вопросов (лист 6).

Марки позиций альбома по видам (продолжение)

Префикс	Что обозначает, позиции	Листы
ДК	декор (картины, зеркала, растения): ДК1–ДК9	1, 61–65
Т	текстиль (шторы, ковры): Т1–Т24	1, 61–65
S	выключатели: S1, S2**, S3–S16	23–30
Р	розетки: Р1–Р6, Р8**, Р11, Р13–Р16, Р17**, Р20**, Р21–Р23, Р26, Р33**, Р34–Р37, Р39, Р41–Р44, Р47, Р48, Р49**, Р50, Р51	23–30
Св	светильники: Св1–Св9, Св10**, Св11–Св14, Св15**, Св16–Св22, Св23**, Св26–Св29, Св30**, Св31–Св39, Св50, Св51, Св52**, Св53–Св61, Св62**, Св64–Св72, Св73**, Св74	23–30
БП	блоки питания LED: БП1–БП6	23–30
ИП	извещатели: ИП1–ИП4, ИП6–ИП8	23–30
LAN	розетки компьютерные: LAN1, LAN3, LAN4, LAN5**	23–30
ТВ	розетки ТВ: ТВ1	23–30
ЩК, ЩС**	щиты: ЩК, ЩС**	23–30
ДФ	домофон: ДФ1	23–30
АР	точки доступа Wi-Fi: АР1**	23–30
ЭВ	выводы кабеля: ЭВ1, ЭВ2, ЭВ4**, ЭВ5**, ЭВ6**, ЭВ7**	23–30
КУП	электроустановочные изделия: КУП1**, КУП2**	23–30
Ст В1, Ст К1, Ст К1-2 (кухня), Ст К1-4 (постирочная), Ст Т3	стояки (системы В1, Т3, К1): Ст В1-1, Ст В1-2, Ст В1-3*, Ст В1-4, Ст К1-1, Ст К1-2 (кухня), Ст К1-3*, Ст К1-4 (постирочная), Ст Т3-1, Ст Т3-2, Ст Т3-3*, Ст Т3-4	33–42
О	марки отделки (реестр альбома): О1–О14	2–5, 78–113
К, КМ	позиции колерной карты: К1–К9, КМ1–КМ5	57–60
РО	радиаторы отопления: РО-1–РО-7	31, 32

Примечания


1. Марка отделки О — одна на весь альбом: одна и та же отделка (материал, изделие, цвет, формат) на всех листах имеет одну марку; на развёртках и планах стоят марки этого реестра.
2. Столбец «Колер. карта» — позиции колерной карты (лист 57): К — окраска по коду цвета, КМ — материал без кода цвета; «Помещения» — номера по экспликации; количества — по ведомости отделки помещений (лист 54).
3. Марки позиций: один префикс — один вид позиций на весь альбом (двери Д, окна ОК, мебель М, сантехприборы П, декор ДК, текстиль Т, колерная карта К и КМ, радиаторы РО, розетки Р, выключатели S, светильники Св; стояки — «Ст» и система, например «Ст К1-1»). Совпадение префиксов у разных видов — замечание к исходным данным, при выпуске исправляется в модели.

Изм.	Кол.уч	Лист	№ док.	Подп.	Дата	ГД-2026-009-АИ			
						Квартира 103 м²			
						Общая площадь 100,72* м² · * размеры со скана, не замерены (реестр — л. 6, 7, К-1)			
Разраб.		Кырлан А.С.			04.11.26	Дизайн-проект интерьера	Стадия	Лист	Листов
Пров.							РП	78	120
ГИП									
Н. контр.						Реестр марок отделки и позиций альбома	Кырлан Александр Сергеевич		
Утв.						М б/м			

выпуск 04.11.2026 № 20cec94f32 · стр. 87 из 130

Схема расположения развёрток и узлов

План квартиры: марки развёрток по помещениям, выноски узлов, ведомость «марка → лист»

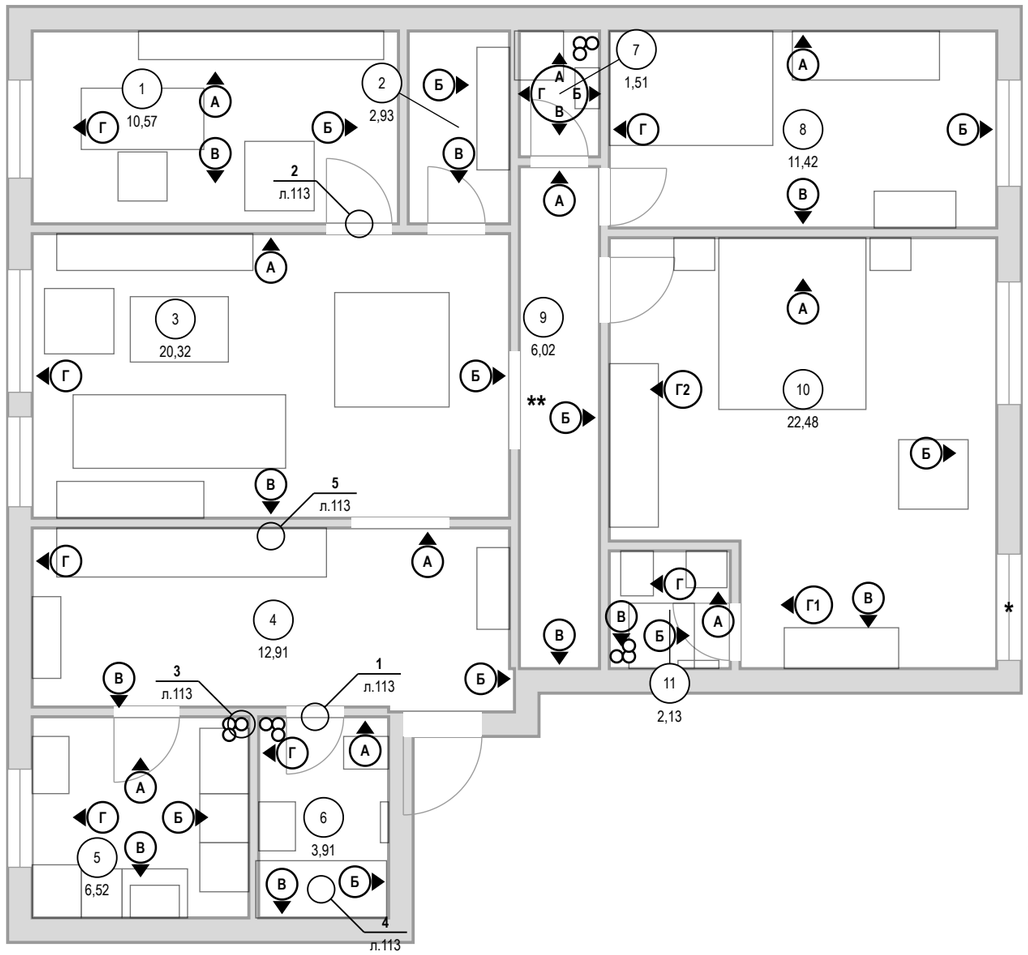

Развёртки и узлы: марка → лист

Марка	Помещение / узел	Лист
А, Б, В, Г	Кабинет-библиотека (пом. 1)	80, 81
Б, В	Кладовая (пом. 2)	82
А, Б, В, Г	Гостиная-столовая (пом. 3)	83–87
А, Б, В, Г	Прихожая-холл (пом. 4)	88–91
Б, В, А, Г	Кухня (пом. 5)	92–94
А, Б, В, Г	Ванная (пом. 6)	95–97
А, Б, В, Г	Постирочная (пом. 7)	98
А, Б, В, Г	Спальня 2 (пом. 8)	99–101
А, Б, В	Коридор (пом. 9)	102–104
А, Б, В, Г1, Г2	Спальня мастер (пом. 10)	105–109
А, Б, В, Г	Ванная мастер (пом. 11)	110–112
узел 1	Порог 15 мм: мокрая зона — смежное помещение	113
узел 2	Дверь скрытого монтажа в плоскости стены, плинтус	113
узел 3	Короб стояков К1-1, К1-2 (кухня) с люком и звукоизоляцией	113
узел 4	Гидроизоляция санузла: заход на стены 200 мм, примыкание ванны	113
узел 5	Плинтус МДФ 83×15 мм у окрашенной стены по доске (ламинату)	113
узел 6	Плинтус МДФ 83×15 мм у окрашенной стены по керамограниту (плитке)	113

Допущения и предложения на листе

Основа листа: размеры сняты со скана обмерного плана KV design (см): часть подписей не читается, помещения выровнены по читаемым размерам; контрольный обмер не выполнен (К-1); высота потолка 2650 мм принята по отметкам обмера (Н = 2,50…2,66 м, ригель 2,28 м) — уточнить при обмере (К-2); толщины стен 300 / 120 мм приняты, межквартирная стена и колонны — по скану, не замерены (К-1); разрешённая мощность 15 кВт принята по типовым ТУ; при объединении двух квартир — переоформление ТУ (К-4); подрайон климата не задан — принят не северный (жилые от 2,5 м) (К-8).

Знак «*» — принято, не замерено и не подтверждено (замерить на объекте): К-1: окно пом. 10 (стена Б) — Окно 1300 при offset 3500 на стене Б основной части (длина 3830) выходило за стену на 970 мм; К-6: Ст К1-3, Ст В1-3, Ст Т3-3 — положение снято со скана обмера, отдельно не замерялось; ось внутри габарита поддона См1 — обмер угла по К-6.

Знак «**» — предложение проектировщика, заказчиком не утверждено (согласовать с заказчиком): К-5: дверь пом. 3 (стена Б) — проём в межквартирной стене — объединение квартир, предложение до техзаключения.

См. лист открытых вопросов (лист 6, записи К-1, К-2, К-4–К-6, К-8).

Условные обозначения

- А — марка развёртки: буква стены, стрелка — взгляд
- выноска узла: над полкой — узел, под полкой — лист
- 1 — номер помещения, площадь м²

1000 мм · печать 1:1

Примечания

1. Развёртки — вид на стену изнутри помещения; буквы стен — одна система на весь альбом (как на листах выводов, плитки и отделки).
2. Стены без электроточек, мебели, декора и акцентной отделки развёрток не имеют: их отделка — по ведомости отделки помещений.
3. Узлы — на листе узлов; места применения — по выноскам этого листа и ведомости «марка → лист».

Изм.	Кол.уч	Лист	№ док.	Подп.	Дата	ГД-2026-009-АИ			
						Квартира 103 м²			
						Общая площадь 100,72* м² · * размеры со скана, не замерены (реестр — л. 6, 7, К-1)			
Разраб.		Кырлан А.С.			04.11.26	Дизайн-проект интерьера	Стадия	Лист	Листов
Пров.							РП	79	120
ГИП									
Н. контр.						Схема расположения развёрток и узлов	Кырлан Александр Сергеевич		
Утв.						М 1:75			


выпуск 04.11.2026 № 20cec94f32 · стр. 88 из 130

Развёртки стен А, Б. Кабинет-библиотека (пом. 1)

Кабинет-библиотека (пом. 1) · вид изнутри помещения · размеры в мм, отметки в м


ПРЕДВАРИТЕЛЬНО · не для производства работ · открыто пунктов: 8 (реестр — л. 6, 7)

Развёртка стены А

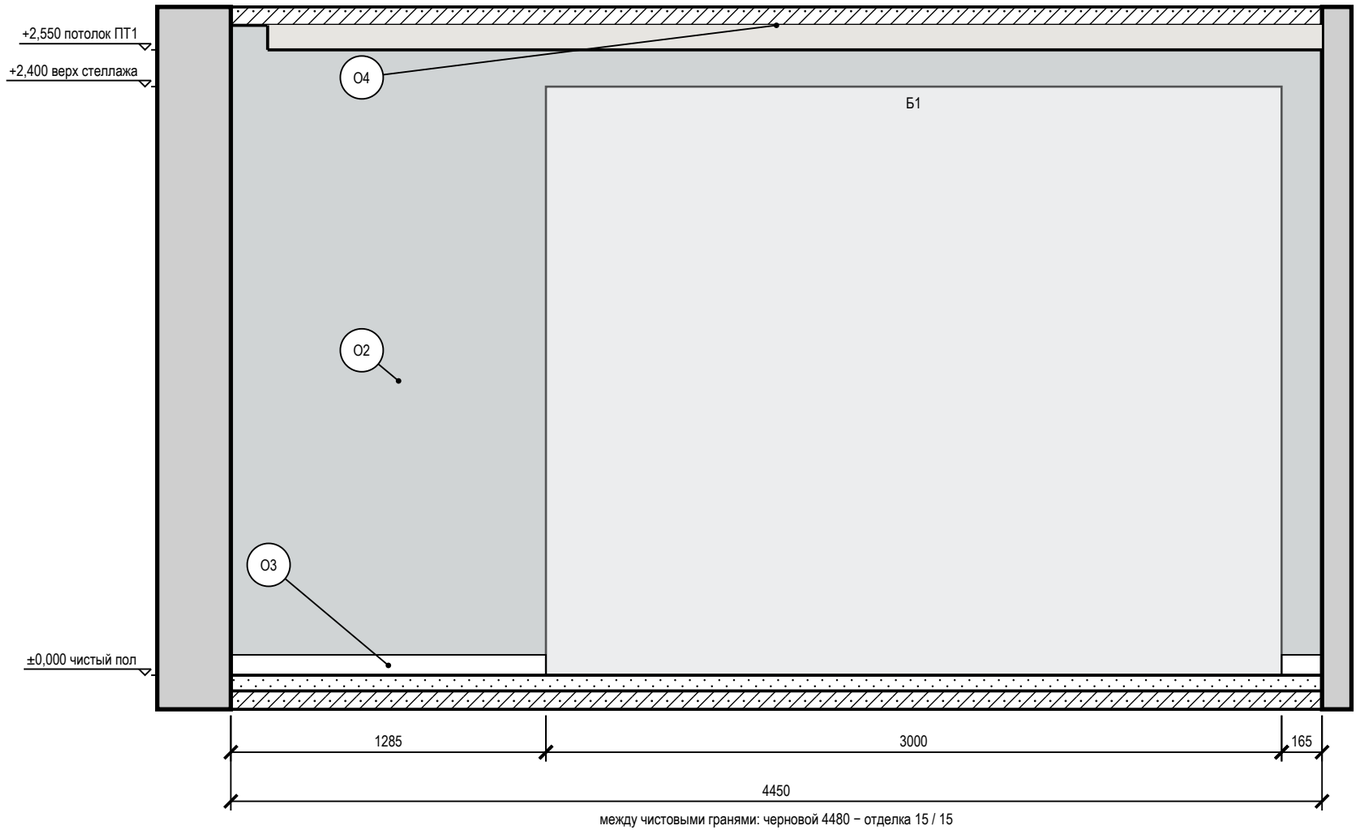


между чистовыми гранями: черновой 4480 − отделка 15 / 15

Развёртка стены Б

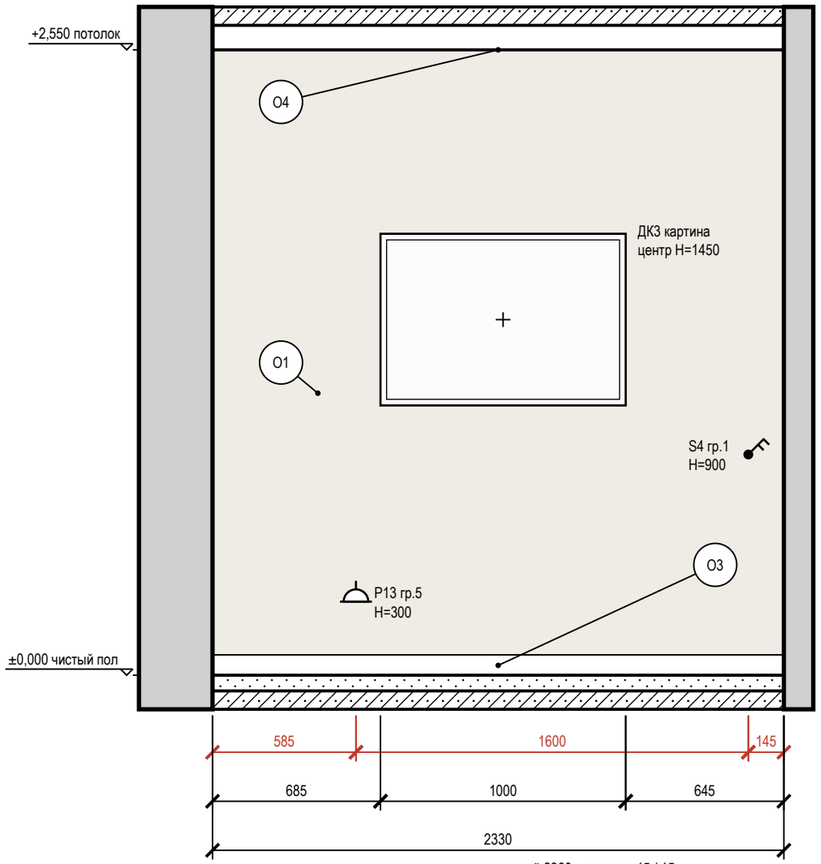

между чистовыми гранями: черновой 2360 − отделка 15 / 15

Схема развёрток (М 1:100)

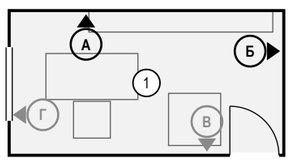

Условные обозначения

- розетка с заземляющим контактом; у знака — марка, ×N постов в рамке, гр. — группа щита, Н — высота оси, мм
- выключатель одноклавишный
- выключатель двухклавишный (флажков — по числу клавиш)
- привязки точек и выводов от угла и от пола, мм
- мебель и приборы — фасад по расстановке (условно)
- картина (декор): марка Д, крест — центр, Н — высота центра, мм
- стены и перекрытия в сечении
- окраска: тон — цвет по коду производителя (условно)
- О1 — марка отделки по реестру отделки альбома
- А — марка развёртки: буква стены, стрелка — взгляд

Допущения и предложения на листе

Основа листа: размеры сняты со скана обмерного плана KV design (см): часть подписей не читается, помещения выровнены по читаемым размерам; контрольный обмер не выполнен (К-1); высота потолка 2650 мм принята по отметкам обмера (Н = 2,50…2,66 м, ригель 2,28 м) — уточнить при обмере (К-2); толщины стен 300 / 120 мм приняты, межквартирная стена и колонны — по скану, не замерены (К-1); разрешённая мощность 15 кВт принята по типовым ТУ; при объединении двух квартир — переоформление ТУ (К-4); подрайон климата не задан — принят не северный (жилые от 2,5 м) (К-8).

См. лист открытых вопросов (лист 6, записи К-1, К-2, К-4, К-8).

Примечания

1. Развёртки — вид на стену изнутри помещения, по часовой стрелке; расположение — на схеме листа и на листе 79; размеры — в мм по чистовым поверхностям; отметки — в м от ±0,000; высоты Н — от чистого пола помещения до оси изделия, у декора — до центра.
2. Красная цепочка — привязки электроточек и выводов по осям от угла чистовых стен; высота Н — у знака, от чистого пола до оси; высоты мебели, проёмов и границ отделки — колонкой отметок слева. Стена с 5 и более точками или с мелкими звеньями привязок показана двумя видами: архитектурная развёртка (мебель, отделка, проёмы, высоты) и вид «Привязки» на отдельном листе — точки и выводы с марками, одна цепочка по осям и таблица привязок (каждая точка — строка).
3. У знака электроточки: марка (Р — розетка, S — выключатель, Св — светильник, ЭВ — вывод кабеля), ×N — число постов в рамке, гр. — группа щита, Н — высота оси от чистого пола, мм; группы по клавишам выключателя — на листе выключателей.
4. Схема мебели, приборов и декора не является технической документацией для производства мебели; габариты — по паспортам изделий.
5. Картины и зеркала крепить к основанию по паспорту изделия (закладные и анкеры — в перечне скрытых работ); крест — ось центра предмета.

1000 мм · печать 1:1

Изм.	Кол.уч	Лист	№ док.	Подп.	Дата
Разраб.		Кырлан А.С.			04.11.26
Пров.					
ГИП					
Н. контр.					
Утв.					

ГД-2026-009-АИ

Квартира 103 м²

Общая площадь 100,72* м² · * размеры со скана, не замерены (реестр — л. 6, 7, К-1)

Дизайн-проект интерьера

Стадия	Лист	Листов
РП	80	120

Развёртки стен А, Б. Кабинет-библиотека (пом. 1)

М 1:25

Кырлан Александр Сергеевич


выпуск 04.11.2026 № 20cec94f32 · стр. 89 из 130

Развёртки стен В, Г. Кабинет-библиотека (пом. 1)

Кабинет-библиотека (пом. 1) · вид изнутри помещения · размеры в мм, отметки в м


ПРЕДВАРИТЕЛЬНО · не для производства работ · открыто пунктов: 8 (реестр — л. 6, 7)

Развёртка стены В

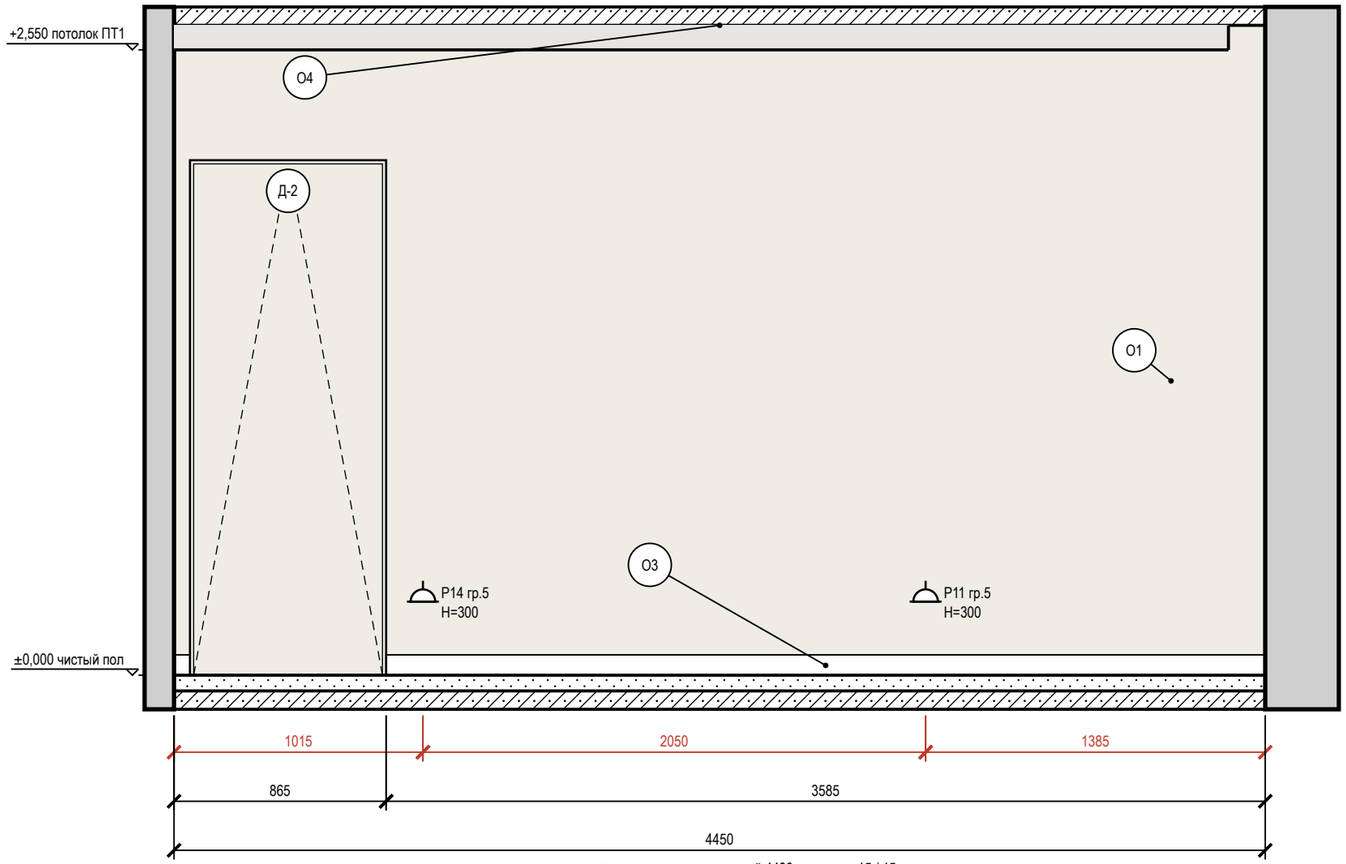


между чистовыми гранями: черновой 4480 − отделка 15 / 15

Развёртка стены Г

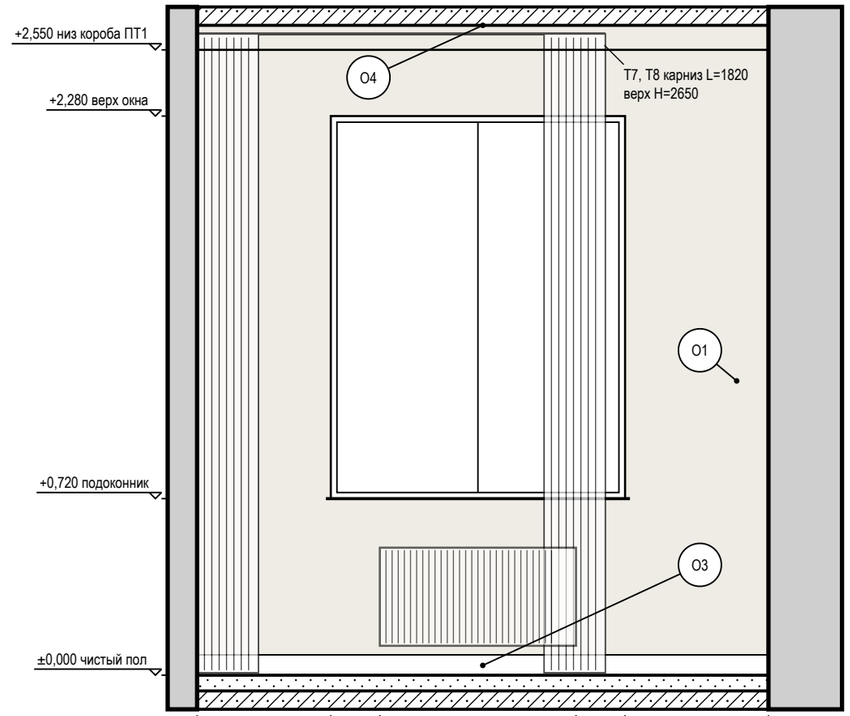

между чистовыми гранями: черновой 2360 − отделка 15 / 15

Схема развёрток (М 1:100)

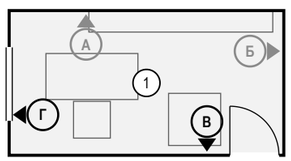

Условные обозначения

- розетка с заземляющим контактом; у знака — марка, ×N постов в рамке, гр. — группа щита, Н — высота оси, мм
- привязки точек и выводов от угла и от пола, мм
- мебель и приборы — фасад по расстановке (условно)
- карниз (шина) и шторы в собранном виде: марка Т, длина L, верх Н
- дверь скрытого монтажа: полотно в плоскости стены (узел — на листе узлов)
- окно: проём, рама, подоконник
- радиатор отопления; марка — по плану отопления
- стены и перекрытия в сечении
- окраска: тон — цвет по коду производителя (условно)
- О1 — марка отделки по реестру отделки альбома
- А — марка развёртки: буква стены, стрелка — взгляд

Допущения и предложения на листе

Основа листа: размеры сняты со скана обмерного плана KV design (см): часть подписей не читается, помещения выровнены по читаемым размерам; контрольный обмер не выполнен (К-1); высота потолка 2650 мм принята по отметкам обмера (Н = 2,50…2,66 м, ригель 2,28 м) — уточнить при обмере (К-2); толщины стен 300 / 120 мм приняты, межквартирная стена и колонны — по скану, не замерены (К-1); разрешённая мощность 15 кВт принята по типовым ТУ; при объединении двух квартир — переоформление ТУ (К-4); подрайон климата не задан — принят не северный (жилые от 2,5 м) (К-8).

См. лист открытых вопросов (лист 6, записи К-1, К-2, К-4, К-8).

Примечания

1. Развёртки — вид на стену изнутри помещения, по часовой стрелке; расположение — на схеме листа и на листе 79; размеры — в мм по чистовым поверхностям; отметки — в м от ±0,000; высоты Н — от чистого пола помещения до оси изделия, у декора — до центра.
2. Красная цепочка — привязки электроточек и выводов по осям от угла чистовых стен; высота Н — у знака, от чистого пола до оси; высоты мебели, проёмов и границ отделки — колонкой отметок слева. Стена с 5 и более точками или с мелкими звеньями привязок показана двумя видами: архитектурная развёртка (мебель, отделка, проёмы, высоты) и вид «Привязки» на отдельном листе — точки и выводы с марками, одна цепочка по осям и таблица привязок (каждая точка — строка).
3. У знака электроточки: марка (Р — розетка, S — выключатель, Св — светильник, ЭВ — вывод кабеля), ×N — число постов в рамке, гр. — группа щита, Н — высота оси от чистого пола, мм; группы по клавишам выключателя — на листе выключателей.
4. Схема мебели, приборов и декора не является технической документацией для производства мебели; габариты — по паспортам изделий.
5. Карнизы (шины) — по ведомости текстиля декоратора: длина L и верх Н на развёртке — те же числа, что в ведомости; крепление — до окраски потолка.
6. Двери скрытого монтажа — полотно в плоскости стены, отделка стены по полотну, плинтус прерывается у короба (узел — на листе узлов).
7. Карниз Т7, Т8: по ведомости текстиля шина L=1820 мм, а от её начала до чистового угла стены — 1665 мм: шина не встаёт, длину согласовать с декоратором до заказа.
8. Линии узора (швы плитки, складки штор, рёбра радиаторов) прерываются у знаков и выносок — просвет между линиями не менее 0,7 мм.

1000 мм · печать 1:1

Изм.	Кол.уч	Лист	№ док.	Подп.	Дата
Разраб.		Кырлан А.С.			04.11.26
Пров.					
ГИП					
Н. контр.					
Утв.					

ГД-2026-009-АИ

Квартира 103 м²

Общая площадь 100,72* м² · * размеры со скана, не замерены (реестр — л. 6, 7, К-1)

Дизайн-проект интерьера

Стадия	Лист	Листов
РП	81	120

Развёртки стен В, Г. Кабинет-библиотека (пом. 1)

М 1:25

Кырлан Александр Сергеевич


выпуск 04.11.2026 № 20cec94f32 · стр. 90 из 130

Развёртки стен. Кладовая (пом. 2)

Кладовая (пом. 2) · вид изнутри помещения · размеры в мм, отметки в м


ПРЕДВАРИТЕЛЬНО · не для производства работ · открыто пунктов: 8 (реестр — л. 6, 7)

Развёртка стены Б

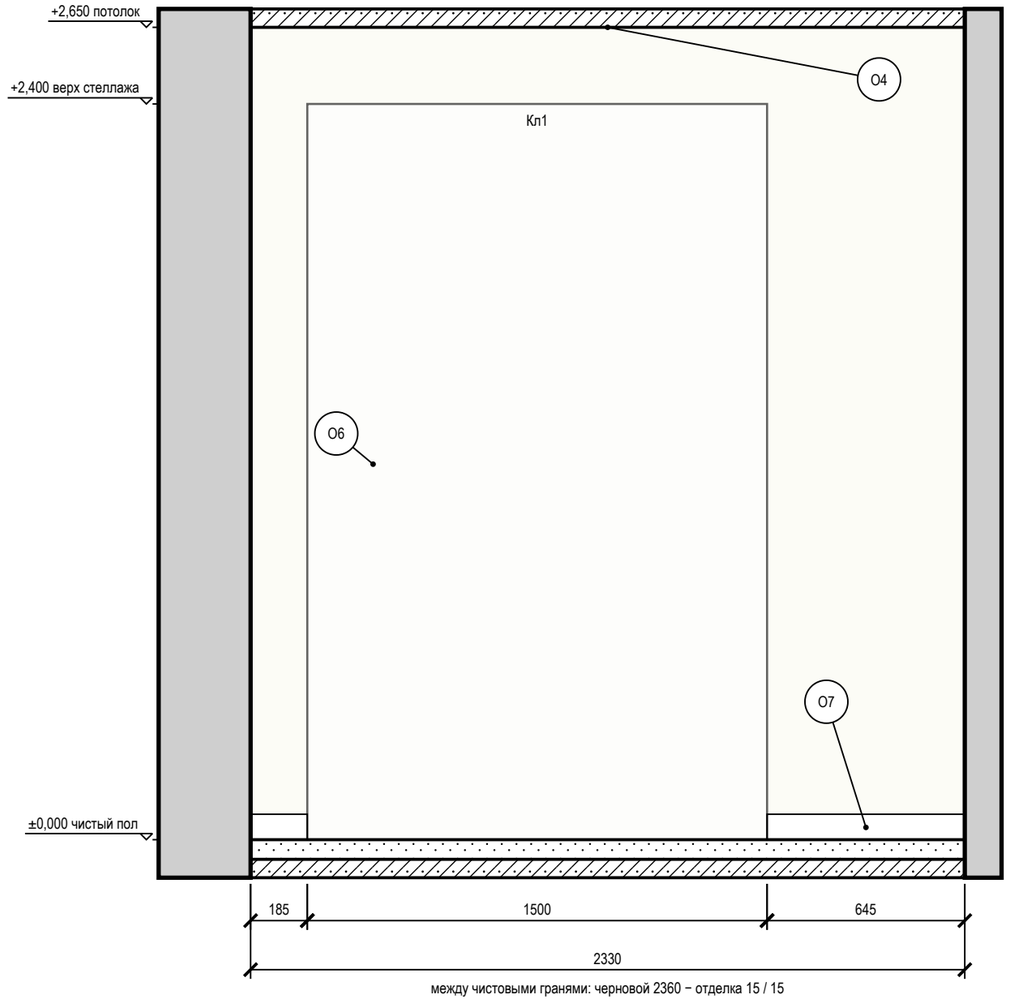


между чистовыми гранями: черновой 2360 − отделка 15 / 15

Развёртка стены В

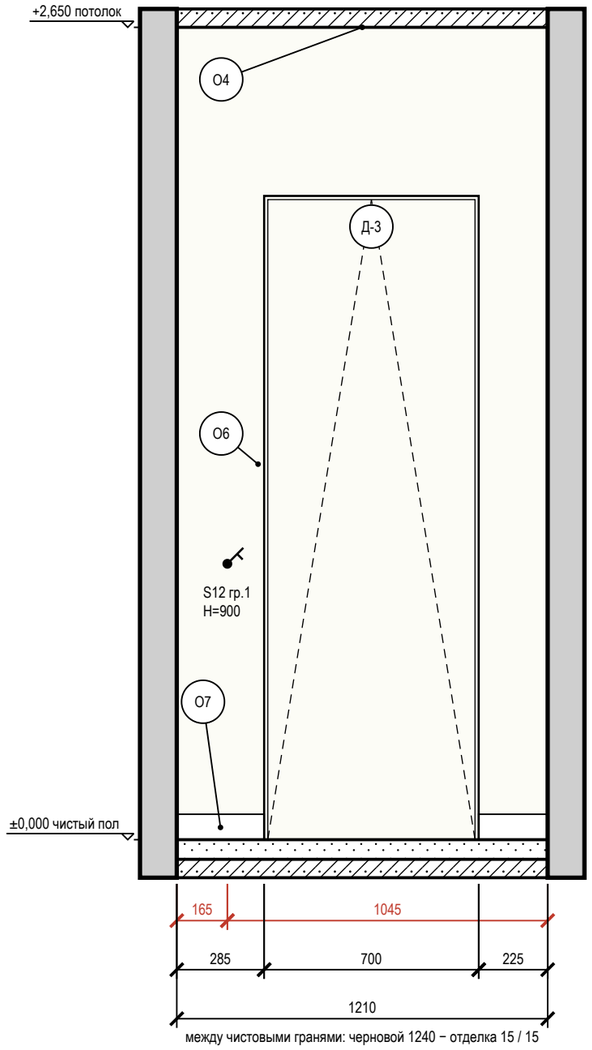

между чистовыми гранями: черновой 1240 − отделка 15 / 15

Схема развёрток (М 1:100)

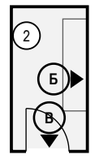

Условные обозначения

- выключатель одноклавишный
- привязки точек и выводов от угла и от пола, мм
- мебель и приборы — фасад по расстановке (условно)
- дверь скрытого монтажа: полотно в плоскости стены (узел — на листе узлов)
- стены и перекрытия в сечении
- окраска: тон — цвет по коду производителя (условно)
- О1 — марка отделки по реестру отделки альбома
- А — марка развёртки: буква стены, стрелка — взгляд

Ведомость отделки (на листе)

Марка	Поверхность	Материал, изделие	Цвет, код	Кол.
О4	потолок	окраска, Tikkurila Anti-Reflex 2, глубокоматовая, подготовка Q3	NCS S 0502-Y «Белый с лёгкой желтизной»	2,9 м²
О6	стены	окраска, Tikkurila Harmony, матовая, подготовка Q3	NCS S 0502-Y «Белый с лёгкой желтизной»	7,9 м²
О7	плинтус	плинтус МДФ, h 83 мм, Ultrawood Base 5340, ЛДФ под окраску, 83×15 мм, 2440 мм (арт. LDF-BASE-5340)	NCS S 0502-Y «Белый с лёгкой желтизной»	1,3 м

Допущения и предложения на листе

Основа листа: размеры сняты со скана обмерного плана KV design (см): часть подписей не читается, помещения выровнены по читаемым размерам; контрольный обмер не выполнен (К-1); высота потолка 2650 мм принята по отметкам обмера (Н = 2,50…2,66 м, ригель 2,28 м) — уточнить при обмере (К-2); толщины стен 300 / 120 мм приняты, межквартирная стена и колонны — по скану, не замерены (К-1); разрешённая мощность 15 кВт принята по типовым ТУ; при объединении двух квартир — переоформление ТУ (К-4); подрайон климата не задан — принят не северный (жилые от 2,5 м) (К-8).

См. лист открытых вопросов (лист 6, записи К-1, К-2, К-4, К-8).

Примечания

1. Развёртки — вид на стену изнутри помещения, по часовой стрелке; расположение — на схеме листа и на листе 79; размеры — в мм по чистовым поверхностям; отметки — в м от ±0,000; высоты Н — от чистого пола помещения до оси изделия, у декора — до центра.
2. Красная цепочка — привязки электроточек и выводов по осям от угла чистовых стен; высота Н — у знака, от чистого пола до оси; высоты мебели, проёмов и границ отделки — колонкой отметок слева. Стена с 5 и более точками или с мелкими звеньями привязок показана двумя видами: архитектурная развёртка (мебель, отделка, проёмы, высоты) и вид «Привязки» на отдельном листе — точки и выводы с марками, одна цепочка по осям и таблица привязок (каждая точка — строка).
3. У знака электроточки: марка (Р — розетка, S — выключатель, Св — светильник, ЭВ — вывод кабеля), ×N — число постов в рамке, гр. — группа щита, Н — высота оси от чистого пола, мм; группы по клавишам выключателя — на листе выключателей.
4. Схема мебели, приборов и декора не является технической документацией для производства мебели; габариты — по паспортам изделий.
5. Двери скрытого монтажа — полотно в плоскости стены, отделка стены по полотну, плинтус прерывается у короба (узел — на листе узлов).

1000 мм · печать 1:1

Изм.	Кол.уч	Лист	№ док.	Подп.	Дата
Разраб.		Кырлан А.С.			04.11.26
Пров.					
ГИП					
Н. контр.					
Утв.					

ГД-2026-009-АИ

Квартира 103 м²

Общая площадь 100,72* м² · * размеры со скана, не замерены (реестр — л. 6, 7, К-1)

Дизайн-проект интерьера

Стадия	Лист	Листов
РП	82	120

Развёртки стен. Кладовая (пом. 2)

М 1:20

Кырлан Александр Сергеевич


выпуск 04.11.2026 № 20cec94f32 · стр. 91 из 130

Развёртка стены А. Гостиная-столовая (пом. 3)

Гостиная-столовая (пом. 3) · вид изнутри помещения · размеры в мм, отметки в м

ПРЕДВАРИТЕЛЬНО · не для производства работ · открыто пунктов: 8 (реестр — л. 6, 7)


Развёртка стены А

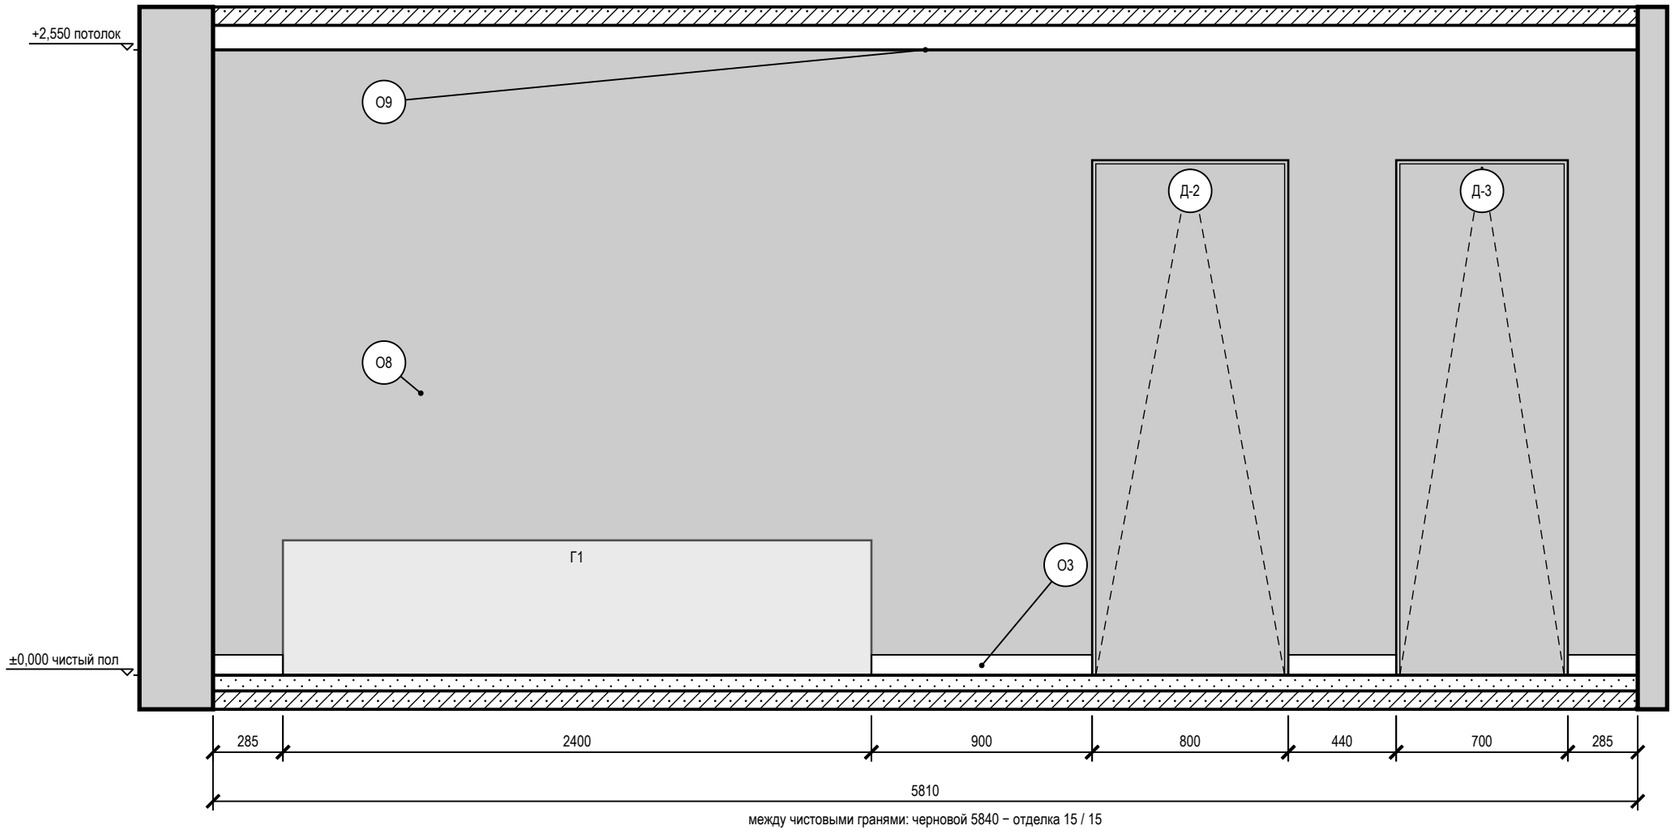

Условные обозначения

- мебель и приборы — фасад по расстановке (условно)
- дверь скрытого монтажа: полотно в плоскости стены (узел — на листе узлов)
- стены и перекрытия в сечении
- окраска: тон — цвет по коду производителя (условно)
- О1 — марка отделки по реестру отделки альбома
- А — марка развёртки: буква стены, стрелка — взгляд

Схема развёрток (М 1:100)

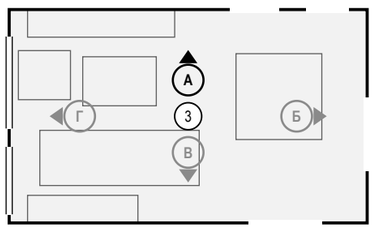

Ведомость отделки (на листе)

Марка	Поверхность	Материал, изделие	Цвет, код	Кол.
О3	плинтус	плинтус МДФ, h 83 мм, Ultrawood Base 5340, ЛДФ под окраску, 83×15 мм, 2440 мм (арт. LDF-BASE-5340), полуглянцевая	Farrow & Ball No. 291 «School House White тёплый меловой белый»	1,9 м
О8	акцентная стена	окраска, Farrow & Ball Modern Emulsion, аналог: интерьерная краска Farrow & Ball Modern Emulsion в цвете веера No. 255, матовая, матовая, подготовка К3	Farrow & Ball No. 255 «Tanner's Brown — тёмный шоколад»	11,7 м²
О9	потолок	окраска, Farrow & Ball Modern Emulsion, матовая, подготовка Q3	Farrow & Ball No. 291 «School House White тёплый меловой белый»	20,3 м²

Допущения и предложения на листе

Основа листа: размеры сняты со скана обмерного плана KV design (см): часть подписей не читается, помещения выровнены по читаемым размерам; контрольный обмер не выполнен (К-1); высота потолка 2650 мм принята по отметкам обмера (Н = 2,50…2,66 м, ригель 2,28 м) — уточнить при обмере (К-2); толщины стен 300 / 120 мм приняты, межквартирная стена и колонны — по скану, не замерены (К-1); разрешённая мощность 15 кВт принята по типовым ТУ; при объединении двух квартир — переоформление ТУ (К-4); подрайон климата не задан — принят не северный (жилые от 2,5 м) (К-8).

Знак («**») — предложение проектировщика, заказчиком не утверждено (согласовать с заказчиком): К-5: дверь пом. 3 (стена Б) — проём в межквартирной стене — объединение квартир, предложение до техзаключения.

См. лист открытых вопросов (лист 6, записи К-1, К-2, К-4, К-5, К-8).

Примечания

1. Развёртки — вид на стену изнутри помещения, по часовой стрелке; расположение — на схеме листа и на листе 79; размеры — в мм по чистовым поверхностям; отметки — в м от ±0,000; высоты Н — от чистого пола помещения до оси изделия, у декора — до центра.
2. Стена А показана двумя видами: здесь — архитектурная развёртка (мебель, отделка, проёмы, высоты), электроточки и выводы ВК с привязками и таблицей — на листе 84 («Привязки»).
3. Схема мебели, приборов и декора не является технической документацией для производства мебели; габариты — по паспортам изделий.
4. Двери скрытого монтажа — полотно в плоскости стены, отделка стены по полотну, плинтус прерывается у короба (узел — на листе узлов).

1000 мм · печать 1:1

Изм.	Кол.уч	Лист	№ док.	Подп.	Дата
Разраб.		Кырлан А.С.			04.11.26
Пров.					
ГИП					
Н. контр.					
Утв.					

ГД-2026-009-АИ

Квартира 103 м²

Общая площадь 100,72* м² · * размеры со скана, не замерены (реестр — л. 6, 7, К-1)

Дизайн-проект интерьера

Стадия	Лист	Листов
РП	83	120

Развёртка стены А. Гостиная-столовая (пом. 3)

М 1:25

Кырлан Александр Сергеевич

выпуск 04.11.2026 № 20cec94f32 · стр. 92 из 130

Привязки электроточек, стена А. Гостиная-столовая (пом. 3)

Гостиная-столовая (пом. 3) · вид изнутри помещения · привязки в мм, отметки в м · к развёртке на листе 83

ПРЕДВАРИТЕЛЬНО · не для производства работ · открыто пунктов: 8 (реестр — л. 6, 7)

Развёртка стены А: электроточки и выводы

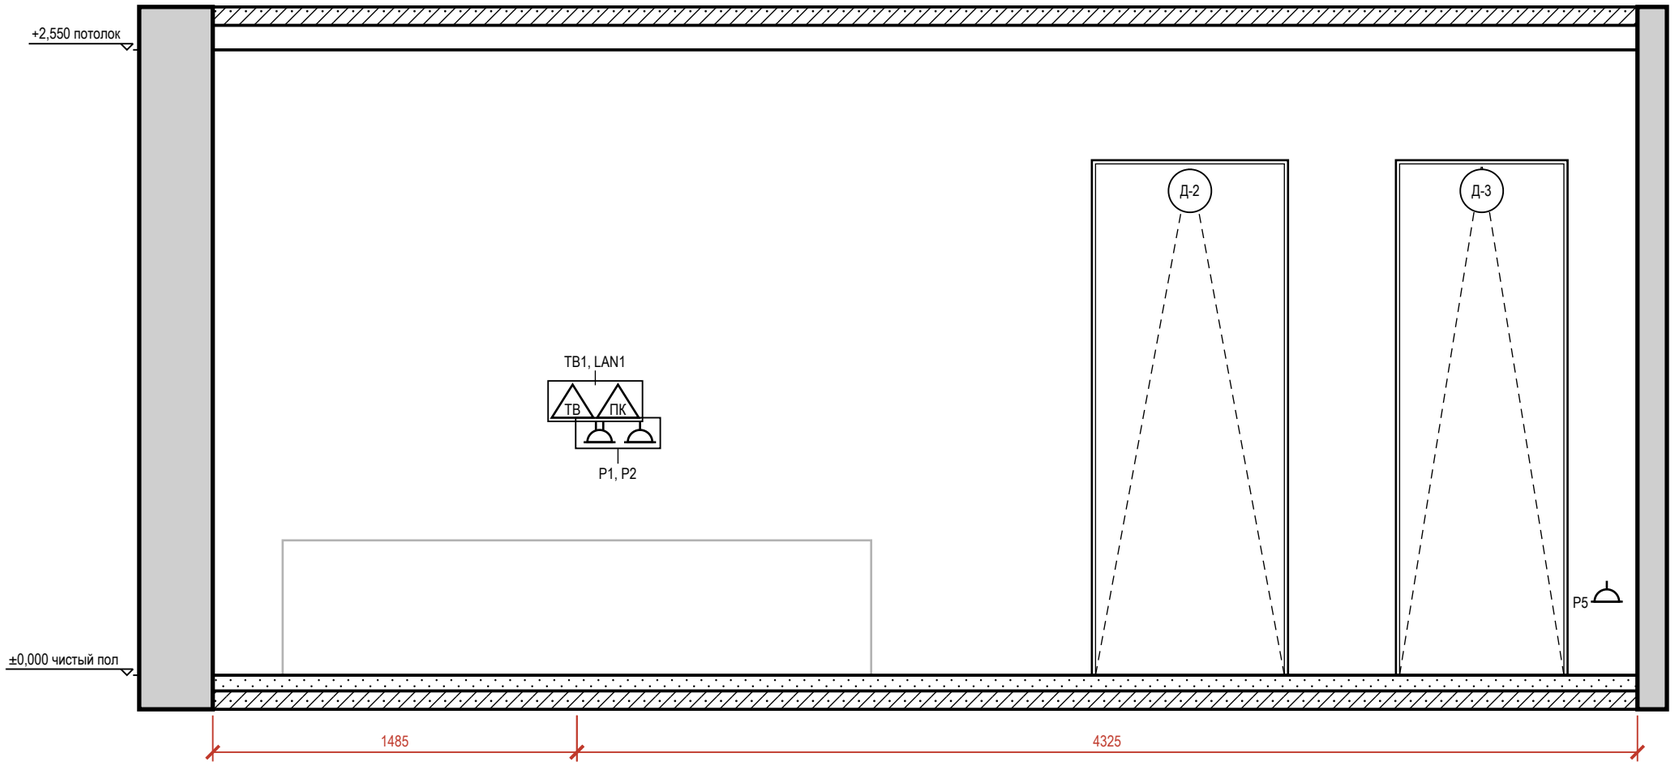



Таблица привязок электроточек и выводов

Марка	Назначение	От угла, мм	Н от пола, мм	Примечание
TB1	розетка ТВ: ТВ-зона	1485	1100	
P1	розетка: ТВ-зона: телевизор, медиаплеер	1585	950	рамка 2 поста, гр. 5
LAN1	розетка RJ45: ТВ-зона: Smart TV	1635	1100	
P2	розетка: ТВ-зона: саундбар	1735	950	гр. 5
P5	розетка: обеденная зона, буфет Г6	5685	300	гр. 5

Условные обозначения

- розетка с заземляющим контактом; у знака — марка, ×N постов в рамке, гр. — группа щита, Н — высота оси, мм
- ПК — розетка компьютерная RJ45
- ТВ — розетка телевизионная
- привязки точек и выводов от угла и от пола, мм
- A — марка развёртки: буква стены, стрелка — взгляд

Схема развёрток (М 1:200)

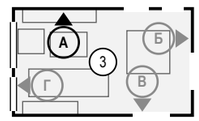

Примечания

1. Вид «Привязки» стены А — электроточки и выводы ВК; архитектурная развёртка (мебель, отделка, проёмы, высоты) — на листе 83, расположение — на листе 79. Мебель и приборы — подложкой для ориентира; их марки и обозначения мебели, проёмов и стен — там же.
2. Привязки — в мм: по горизонтали от левого чистового угла стены до оси изделия, Н — от чистого пола до оси; все точки — в таблице привязок. Красная цепочка — привязки по осям; точки ближе 150 мм одна к другой в цепочку не дробятся — их привязки только в таблице.
3. У знака — марка электроточки (Р — розетка, S — выключатель, Св — светильник, ЭВ — вывод кабеля); посты в рамке и группа щита — в графе «Примечание»; группы по клавишам выключателя — на листе выключателей.

Допущения и предложения на листе

Основа листа: размеры сняты со скана обмерного плана KV design (см): часть подписей не читается, помещения выровнены по читаемым размерам; контрольный обмер не выполнен (К-1); высота потолка 2650 мм принята по отметкам обмера (Н = 2,50…2,66 м, ригель 2,28 м) — уточнить при обмере (К-2); толщины стен 300 / 120 мм приняты, межквартирная стена и колонны — по скану, не замерены (К-1); разрешённая мощность 15 кВт принята по типовым ТУ; при объединении двух квартир — переоформление ТУ (К-4); подрайон климата не задан — принят не северный (жилые от 2,5 м) (К-8).

Знак «**» — предложение проектировщика, заказчиком не утверждено (согласовать с заказчиком): К-5: дверь пом. 3 (стена Б) — проём в межквартирной стене — объединение квартир, предложение до техзаключения.

См. лист открытых вопросов (лист 6, записи К-1, К-2, К-4, К-5, К-8).

1000 мм · печать 1:1

Изм.	Кол.уч	Лист	№ док.	Подп.	Дата
Разраб.		Кырлан А.С.			04.11.26
Пров.					
ГИП					
Н. контр.					
Утв.					

ГД-2026-009-АИ

Квартира 103 м²

Общая площадь 100,72* м² · * размеры со скана, не замерены (реестр — л. 6, 7, К-1)

Дизайн-проект интерьера

Стадия	Лист	Листов
РП	84	120

Привязки электроточек, стена А. Гостиная-столовая (пом. 3)

М 1:25

Кырлан Александр Сергеевич


выпуск 04.11.2026 № 20cec94f32 · стр. 93 из 130

Развёртка стены Б. Гостиная-столовая (пом. 3)

Гостиная-столовая (пом. 3) · вид изнутри помещения · размеры в мм, отметки в м

ПРЕДВАРИТЕЛЬНО · не для производства работ · открыто пунктов: 8 (реестр — л. 6, 7)

Развёртка стены Б

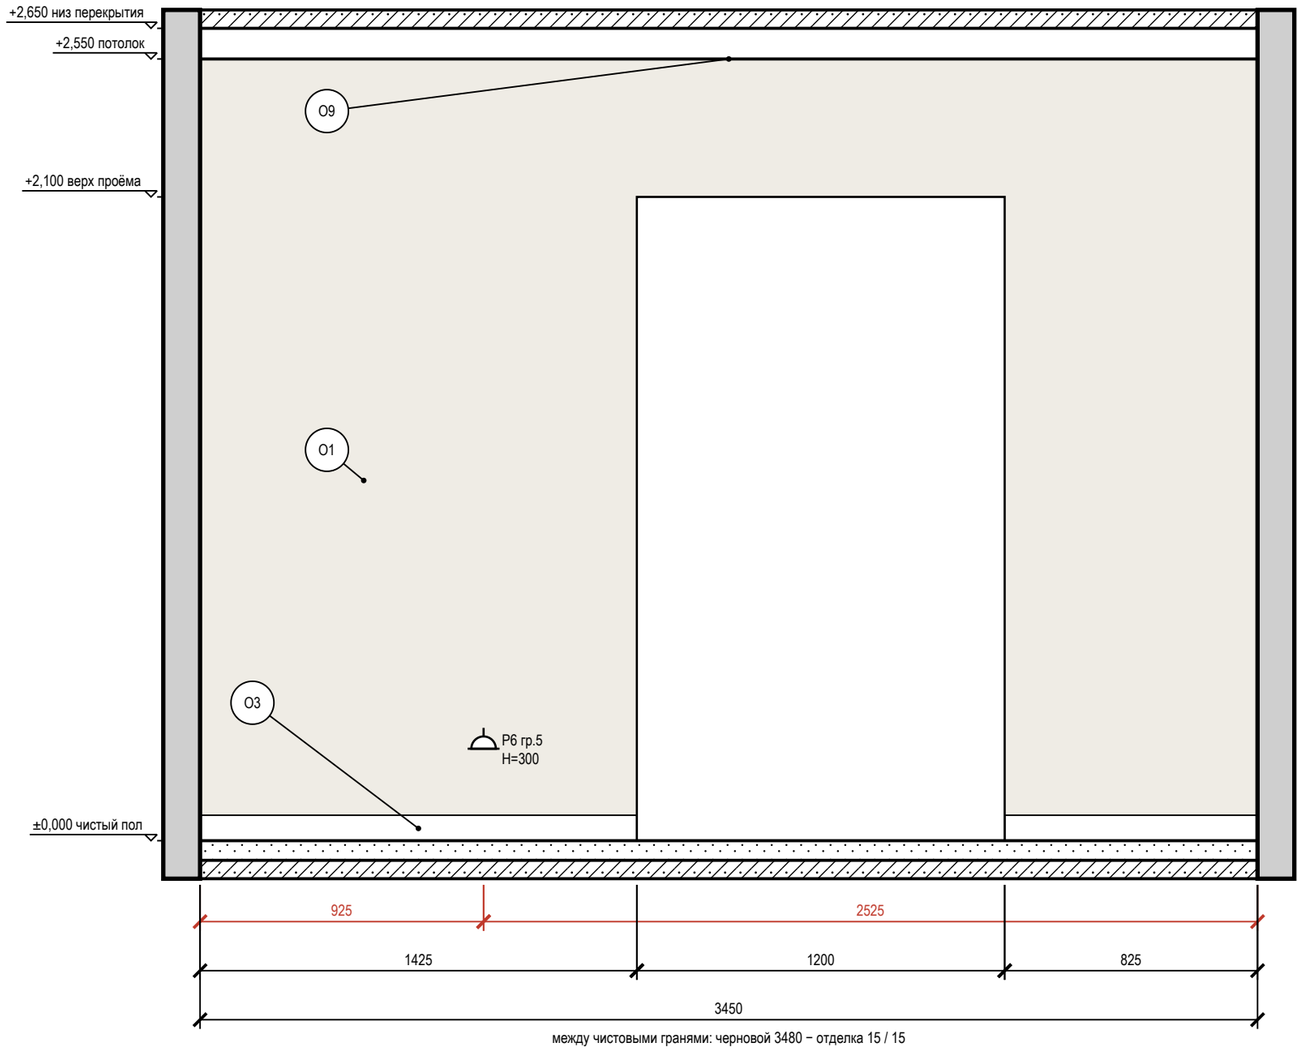

между чистовыми гранями: черновой 3480 − отделка 15 / 15

Допущения и предложения на листе

Основа листа: размеры сняты со скана обмерного плана KV design (см): часть подписей не читается, помещения выровнены по читаемым размерам; контрольный обмер не выполнен (К-1); высота потолка 2650 мм принята по отметкам обмера (Н = 2,50…2,66 м, ригель 2,28 м) — уточнить при обмере (К-2); толщины стен 300 / 120 мм приняты, межквартирная стена и колонны — по скану, не замерены (К-1); разрешённая мощность 15 кВт принята по типовым ТУ; при объединении двух квартир — переоформление ТУ (К-4); подрайон климата не задан — принят не северный (жилые от 2,5 м) (К-8).

Знак «**» — предложение проектировщика, заказчиком не утверждено (согласовать с заказчиком): К-5: дверь пом. 3 (стена Б) — проём в межквартирной стене — объединение квартир, предложение до техзаключения.


См. лист открытых вопросов (лист 6, записи К-1, К-2, К-4, К-5, К-8).

Примечания

1. Развёртки — вид на стену изнутри помещения, по часовой стрелке; расположение — на схеме листа и на листе 79; размеры — в мм по чистовым поверхностям; отметки — в м от ±0,000; высоты Н — от чистого пола помещения до оси изделия, у декора — до центра.
2. Красная цепочка — привязки электроточек и выводов по осям от угла чистовых стен; высота Н — у знака, от чистого пола до оси; высоты мебели, проёмов и границ отделки — колонкой отметок слева. Стена с 5 и более точками или с мелкими звеньями привязок показана двумя видами: архитектурная развёртка (мебель, отделка, проёмы, высоты) и вид «Привязки» на отдельном листе — точки и выводы с марками, одна цепочка по осям и таблица привязок (каждая точка — строка).
3. У знака электроточки: марка (Р — розетка, S — выключатель, Св — светильник, ЭВ — вывод кабеля), ×N — число постов в рамке, гр. — группа щита, Н — высота оси от чистого пола, мм; группы по клавишам выключателя — на листе выключателей.
4. Схема мебели, приборов и декора не является технической документацией для производства мебели; габариты — по паспортам изделий.

1000 мм · печать 1:1

Схема развёрток (М 1:100)

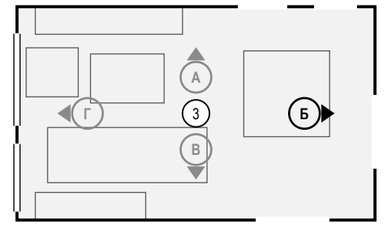

Условные обозначения

- розетка с заземляющим контактом; у знака — марка, ×N постов в рамке, гр. — группа щита, Н — высота оси, мм
- привязки точек и выводов от угла и от пола, мм
- мебель и приборы — фасад по расстановке (условно)
- дверной проём; марка двери — в кружке
- стены и перекрытия в сечении
- окраска: тон — цвет по коду производителя (условно)
- О1 — марка отделки по реестру отделки альбома
- А — марка развёртки: буква стены, стрелка — взгляд

Ведомость отделки (на листе)

Марка	Поверхность	Материал, изделие	Цвет, код	Кол.
О1	стены	окраска, Farrow & Ball Modern Emulsion, матовая, подготовка К3	Farrow & Ball No. 291 «School House White — тёплый меловой белый»	6,3 м²
О3	плинтус	плинтус МДФ, h 83 мм, Ultrawood Base 5340, ЛДФ под окраску, 83×15 мм, 2440 мм (арт. LDF-BASE-5340), полуглянцевая	Farrow & Ball No. 291 «School House White — тёплый меловой белый»	2,3 м
О9	потолок	окраска, Farrow & Ball Modern Emulsion, матовая, подготовка Q3	Farrow & Ball No. 291 «School House White — тёплый меловой белый»	20,3 м²

Изм.	Кол.уч	Лист	№ док.	Подп.	Дата
Разраб.		Кырлан А.С.			04.11.26
Пров.					
ГИП					
Н. контр.					
Утв.					

ГД-2026-009-АИ

Квартира 103 м²

Общая площадь 100,72* м² · * размеры со скана, не замерены (реестр — л. 6, 7, К-1)

Дизайн-проект интерьера

Стадия	Лист	Листов
РП	85	120

Развёртка стены Б. Гостиная-столовая (пом. 3)

М 1:20

Кырлан Александр Сергеевич


выпуск 04.11.2026 № 20cec94f32 · стр. 94 из 130

Развёртка стены В. Гостиная-столовая (пом. 3)

Гостиная-столовая (пом. 3) · вид изнутри помещения · размеры в мм, отметки в м


ПРЕДВАРИТЕЛЬНО · не для производства работ · открыто пунктов: 8 (реестр — л. 6, 7)

Развёртка стены В

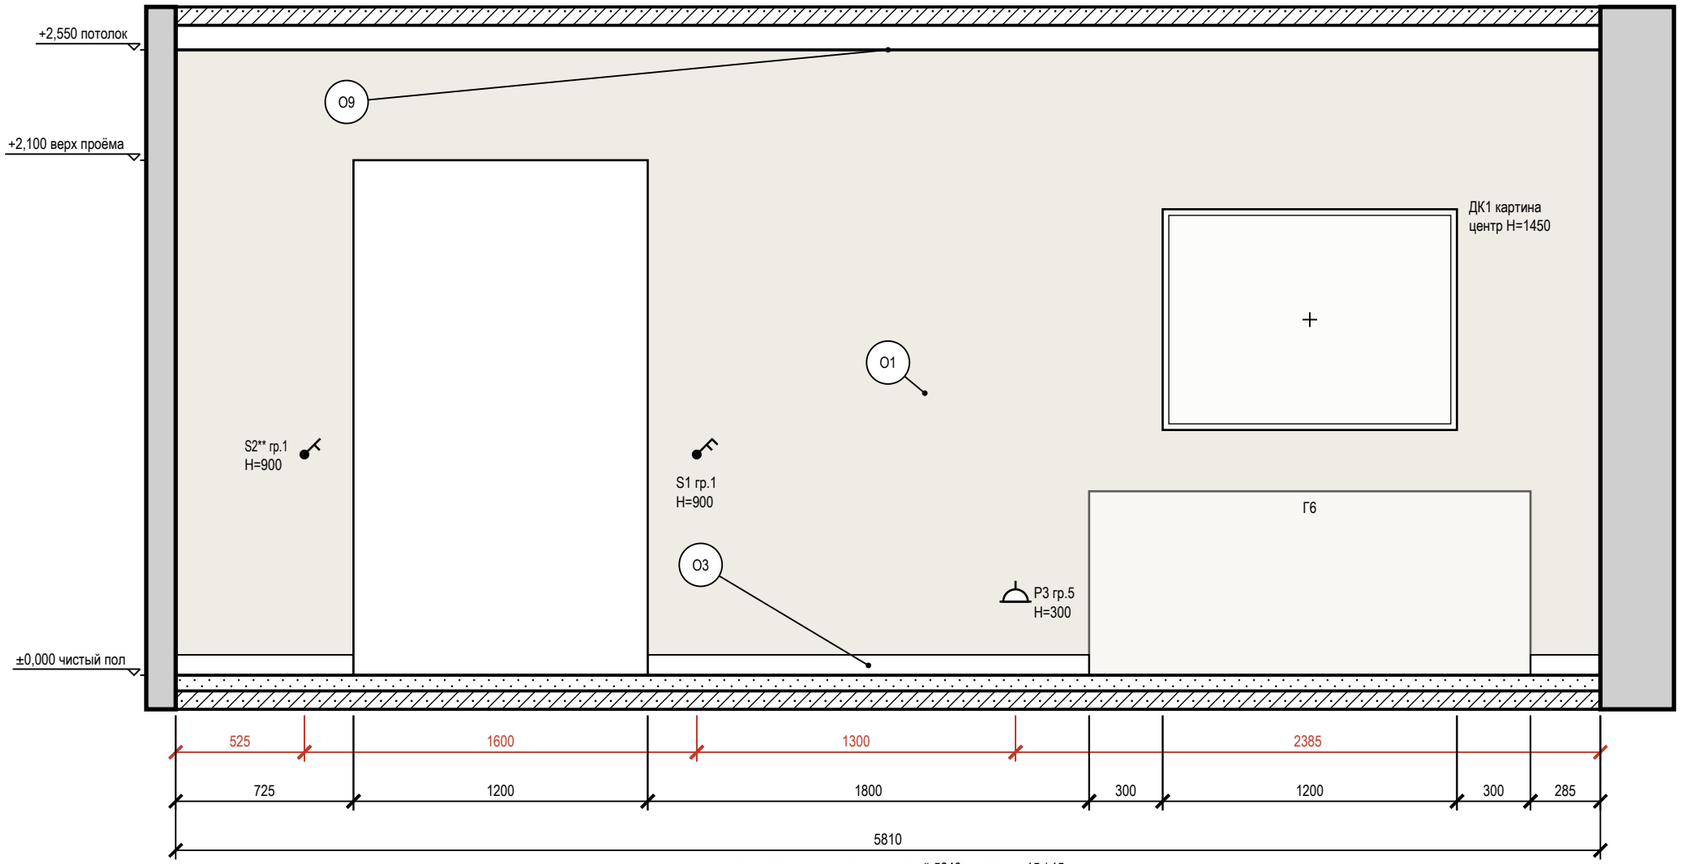

между чистовыми гранями: черновой 5840 − отделка 15 / 15

Схема развёрток (М 1:100)

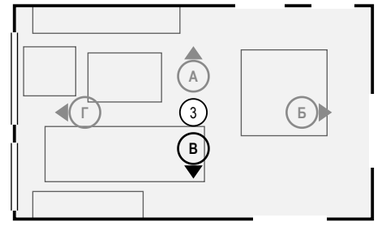

Условные обозначения

- розетка с заземляющим контактом; у знака — марка, ×N постов в рамке, гр. — группа щита, Н — высота оси, мм
- выключатель одноклавишный
- выключатель двухклавишный (флажков — по числу клавиш)
- привязки точек и выводов от угла и от пола, мм
- мебель и приборы — фасад по расстановке (условно)
- картина (декор): марка Д, крест — центр, Н — высота центра, мм
- дверной проём; марка двери — в кружке
- стены и перекрытия в сечении
- окраска: тон — цвет по коду производителя (условно)
- О1 — марка отделки по реестру отделки альбома
- А — марка развёртки: буква стены, стрелка — взгляд

Допущения и предложения на листе

Основа листа: размеры сняты со скана обмерного плана KV design (см): часть подписей не читается, помещения выровнены по читаемым размерам; контрольный обмер не выполнен (К-1); высота потолка 2650 мм принята по отметкам обмера (Н = 2,50…2,66 м, ригель 2,28 м) — уточнить при обмере (К-2); толщины стен 300 / 120 мм приняты, межквартирная стена и колонны — по скану, не замерены (К-1); разрешённая мощность 15 кВт принята по типовым ТУ; при объединении двух квартир — переоформление ТУ (К-4); подрайон климата не задан — принят не северный (жилые от 2,5 м) (К-8).

Знак «**» — предложение проектировщика, заказчиком не утверждено (согласовать с заказчиком): S2 — светорегулятор добавлен под диммируемую ленту L3; уровни сценариев выбраны конвейером; К-5: дверь пом. 3 (стена Б) — проём в межквартирной стене — объединение квартир, предложение до техзаключения.

См. лист открытых вопросов (лист 6, записи К-1, К-2, К-4, К-5, К-8).

Примечания

1. Развёртки — вид на стену изнутри помещения, по часовой стрелке; расположение — на схеме листа и на листе 79; размеры — в мм по чистовым поверхностям; отметки — в м от ±0,000; высоты Н — от чистого пола помещения до оси изделия, у декора — до центра.
2. Красная цепочка — привязки электроточек и выводов по осям от угла чистовых стен; высота Н — у знака, от чистого пола до оси; высоты мебели, проёмов и границ отделки — колонкой отметок слева. Стена с 5 и более точками или с мелкими звеньями привязок показана двумя видами: архитектурная развёртка (мебель, отделка, проёмы, высоты) и вид «Привязки» на отдельном листе — точки и выводы с марками, одна цепочка по осям и таблица привязок (каждая точка — строка).
3. У знака электроточки: марка (Р — розетка, S — выключатель, Св — светильник, ЭВ — вывод кабеля), ×N — число постов в рамке, гр. — группа щита, Н — высота оси от чистого пола, мм; группы по клавишам выключателя — на листе выключателей.
4. Схема мебели, приборов и декора не является технической документацией для производства мебели; габариты — по паспортам изделий.
5. Картины и зеркала крепить к основанию по паспорту изделия (закладные и анкеры — в перечне скрытых работ); крест — ось центра предмета.

1000 мм · печать 1:1

Изм.	Кол.уч	Лист	№ док.	Подп.	Дата
Разраб.		Кырлан А.С.			04.11.26
Пров.					
ГИП					
Н. контр.					
Утв.					

ГД-2026-009-АИ

Квартира 103 м²

Общая площадь 100,72* м² · * размеры со скана, не замерены (реестр — л. 6, 7, К-1)

Дизайн-проект интерьера	Стадия	Лист	Листов
	РП	86	120

Развёртка стены В. Гостиная-столовая (пом. 3)

М 1:25

Кырлан Александр Сергеевич

выпуск 04.11.2026 № 20cec94f32 · стр. 95 из 130

Развёртка стены Г. Гостиная-столовая (пом. 3)

Гостиная-столовая (пом. 3) · вид изнутри помещения · размеры в мм, отметки в м

Развёртка стены Г


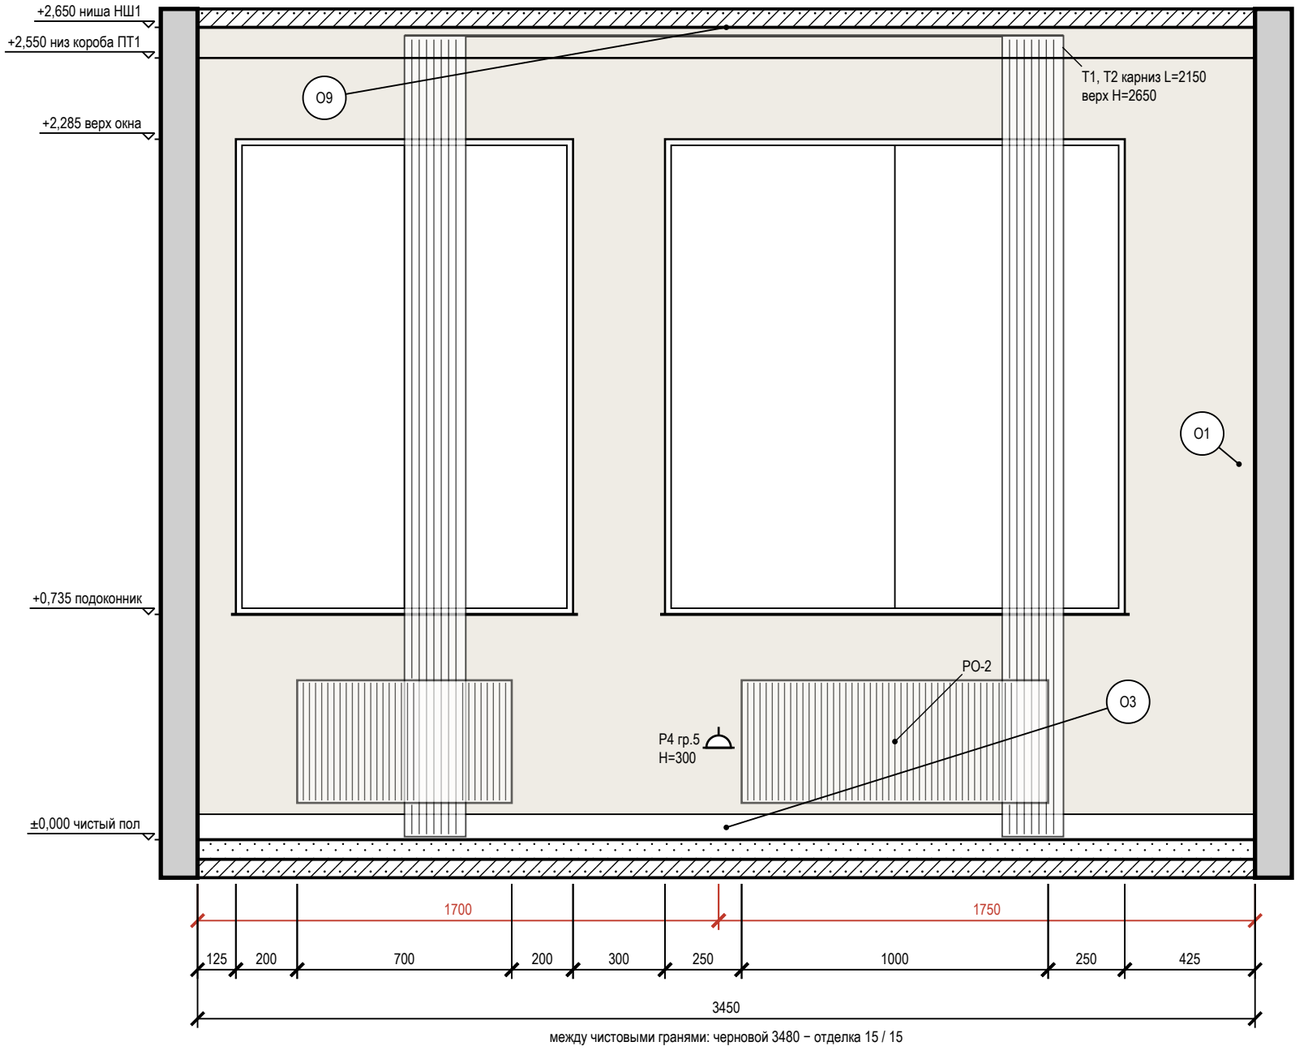


Схема развёрток (М 1:100)

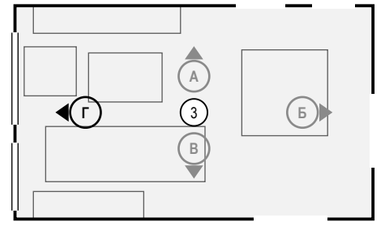

Условные обозначения

- розетка с заземляющим контактом; у знака — марка, ×N постов в рамке, гр. — группа щита, Н — высота оси, мм
- привязки точек и выводов от угла и от пола, мм
- мебель и приборы — фасад по расстановке (условно)
- карниз (шина) и шторы в собранном виде: марка Т, длина L, верх Н
- окно: проём, рама, подоконник
- радиатор отопления; марка — по плану отопления
- стены и перекрытия в сечении
- окраска: тон — цвет по коду производителя (условно)
- О1 — марка отделки по реестру отделки альбома
- А — марка развёртки: буква стены, стрелка — взгляд

Ведомость отделки (на листе)

Марка	Поверхность	Материал, изделие	Цвет, код	Кол.
О1	стены	окраска, Farrow & Ball Modern Emulsion, матовая, подготовка К3	Farrow & Ball No. 291 «School House White — тёплый меловой белый»	5,1 м²
О3	плинтус	плинтус МДФ, h 83 мм, Ultrawood Base 5340, ЛДФ под окраску, 83×15 мм, 2440 мм (арт. LDF-BASE-5340), полуглянцевая	Farrow & Ball No. 291 «School House White — тёплый меловой белый»	3,5 м
О9	потолок	окраска, Farrow & Ball Modern Emulsion, матовая, подготовка Q3	Farrow & Ball No. 291 «School House White — тёплый меловой белый»	20,3 м²

Допущения и предложения на листе

Основа листа: размеры сняты со скана обмерного плана KV design (см): часть подписей не читается, помещения выровнены по читаемым размерам; контрольный обмер не выполнен (К-1); высота потолка 2650 мм принята по отметкам обмера (Н = 2,50…2,66 м, ригель 2,28 м) — уточнить при обмере (К-2); толщины стен 300 / 120 мм приняты, межквартирная стена и колонны — по скану, не замерены (К-1); разрешённая мощность 15 кВт принята по типовым ТУ; при объединении двух квартир — переоформление ТУ (К-4); подрайон климата не задан — принят не северный (жилые от 2,5 м) (К-8).

Знак «**» — предложение проектировщика, заказчиком не утверждено (согласовать с заказчиком): К-5: дверь пом. 3 (стена Б) — проём в межквартирной стене — объединение квартир, предложение до техзаключения.

См. лист открытых вопросов (лист 6, записи К-1, К-2, К-4, К-5, К-8).

Примечания

1. Развёртки — вид на стену изнутри помещения, по часовой стрелке; расположение — на схеме листа и на листе 79; размеры — в мм по чистовым поверхностям; отметки — в м от ±0,000; высоты Н — от чистого пола помещения до оси изделия, у декора — до центра.
2. Красная цепочка — привязки электроточек и выводов по осям от угла чистовых стен; высота Н — у знака, от чистого пола до оси; высоты мебели, проёмов и границ отделки — колонкой отметок слева. Стена с 5 и более точками или с мелкими звеньями привязок показана двумя видами: архитектурная развёртка (мебель, отделка, проёмы, высоты) и вид «Привязки» на отдельном листе — точки и выводы с марками, одна цепочка по осям и таблица привязок (каждая точка — строка).
3. У знака электроточки: марка (Р — розетка, S — выключатель, Св — светильник, ЭВ — вывод кабеля), ×N — число постов в рамке, гр. — группа щита, Н — высота оси от чистого пола, мм; группы по клавишам выключателя — на листе выключателей.
4. Схема мебели, приборов и декора не является технической документацией для производства мебели; габариты — по паспортам изделий.
5. Карнизы (шины) — по ведомости текстиля декоратора: длина L и верх Н на развёртке — те же числа, что в ведомости; крепление — до окраски потолка.
6. Линии узора (швы плитки, складки штор, рёбра радиаторов) прерываются у знаков и выносок — просвет между линиями не менее 0,7 мм.

1000 мм · печать 1:1

Изм.	Кол.уч	Лист	№ док.	Подп.	Дата
Разраб.		Кырлан А.С.			04.11.26
Пров.					
ГИП					
Н. контр.					
Утв.					

ГД-2026-009-АИ

Квартира 103 м²

Общая площадь 100,72* м² · * размеры со скана, не замерены (реестр — л. 6, 7, К-1)

Дизайн-проект интерьера	Стадия	Лист	Листов
	РП	87	120

Развёртка стены Г. Гостиная-столовая (пом. 3)

М 1:20

Кырлан Александр Сергеевич


выпуск 04.11.2026 № 20cec94f32 · стр. 96 из 130

Развёртка стены А. Прихожая-холл (пом. 4)

ПРЕДВАРИТЕЛЬНО · не для производства работ · открыто пунктов: 8 (реестр — л. 6, 7)


Прихожая-холл (пом. 4) · вид изнутри помещения · размеры в мм, отметки в м

Развёртка стены А

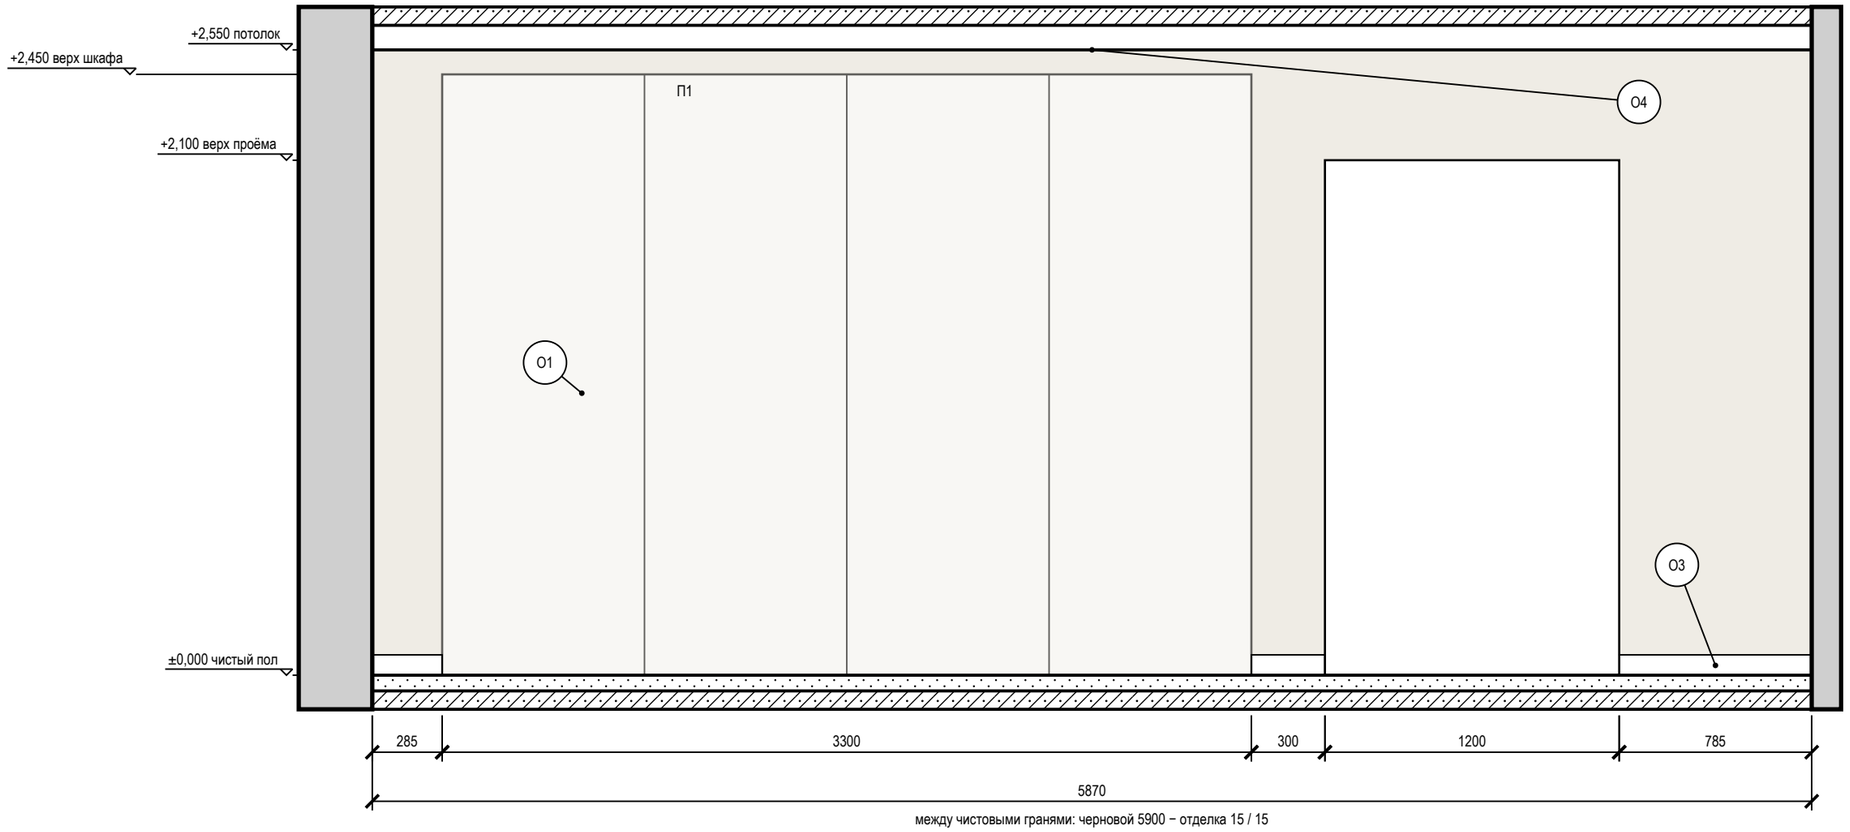

между чистовыми гранями: черновой 5900 − отделка 15 / 15

Схема развёрток (М 1:100)

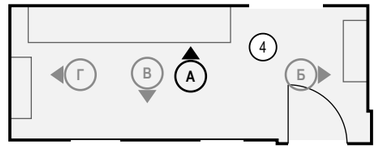

Условные обозначения

- мебель и приборы — фасад по расстановке (условно)
- дверной проём; марка двери — в кружке
- стены и перекрытия в сечении
- окраска: тон — цвет по коду производителя (условно)
- О1 — марка отделки по реестру отделки альбома
- А — марка развёртки: буква стены, стрелка — взгляд

Ведомость отделки (на листе)

Марка	Поверхность	Материал, изделие	Цвет, код	Кол.
О1	стены	окраска, Farrow & Ball Modern Emulsion, матовая, подготовка Q3	Farrow & Ball No. 291 «School House White тёплый меловой белый»	12,4 м²
О3	плинтус	плинтус МДФ, h 83 мм, Ultrawood Base 5340, ЛДФ под окраску, 83×15 мм, 2440 мм (арт. LDF-BASE-5340)	Farrow & Ball No. 291 «School House White тёплый меловой белый»	1,4 м
О4	потолок	окраска, Tikkurila Anti-Reflex 2, глубокоматовая, подготовка Q3	NCS S 0502-Y «Белый с лёгкой желтизной»	12,9 м²

Примечания

1. Развёртки — вид на стену изнутри помещения, по часовой стрелке; расположение — на схеме листа и на листе 79; размеры — в мм по чистовым поверхностям; отметки — в м от ±0,000; высоты Н — от чистого пола помещения до оси изделия, у декора — до центра.
2. Схема мебели, приборов и декора не является технической документацией для производства мебели; габариты — по паспортам изделий.

Допущения и предложения на листе

Основа листа: размеры сняты со скана обмерного плана KV design (см): часть подписей не читается, помещения выровнены по читаемым размерам; контрольный обмер не выполнен (К-1); высота потолка 2650 мм принята по отметкам обмера (Н = 2,50…2,66 м, ригель 2,28 м) — уточнить при обмере (К-2); толщины стен 300 / 120 мм приняты, межквартирная стена и колонны — по скану, не замерены (К-1); разрешённая мощность 15 кВт принята по типовым ТУ; при объединении двух квартир — переоформление ТУ (К-4); подрайон климата не задан — принят не северный (жилые от 2,5 м) (К-8).
См. лист открытых вопросов (лист 6, записи К-1, К-2, К-4, К-8).

1000 мм · печать 1:1

Изм.	Кол.уч	Лист	№ док.	Подп.	Дата
Разраб.		Кырлан А.С.			04.11.26
Пров.					
ГИП					
Н. контр.					
Утв.					

ГД-2026-009-АИ

Квартира 103 м²

Общая площадь 100,72* м² · * размеры со скана, не замерены (реестр — л. 6, 7, К-1)

Дизайн-проект интерьера

Стадия	Лист	Листов
РП	88	120

Развёртка стены А. Прихожая-холл (пом. 4)

М 1:25

Кырлан Александр Сергеевич


выпуск 04.11.2026 № 20cec94f32 · стр. 97 из 130

Развёртка стены Б. Прихожая-холл (пом. 4)

Прихожая-холл (пом. 4) · вид изнутри помещения · размеры в мм, отметки в м


ПРЕДВАРИТЕЛЬНО · не для производства работ · открыто пунктов: 8 (реестр — л. 6, 7)

Развёртка стены Б

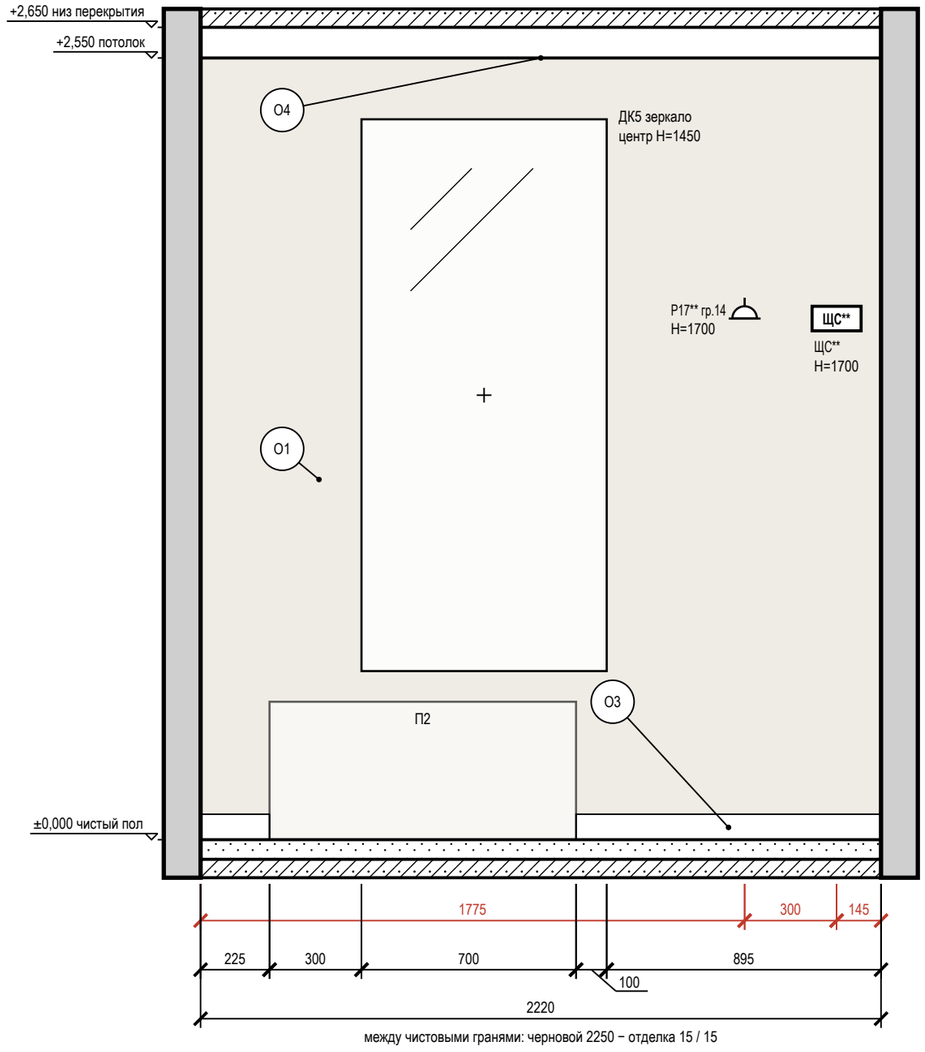

между чистовыми гранями: черновой 2250 − отделка 15 / 15

Схема развёрток (М 1:100)

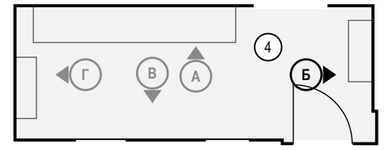

Условные обозначения

- розетка с заземляющим контактом; у знака — марка, ×N постов в рамке, гр. — группа щита, Н — высота оси, мм
- ЩК — щит квартирный
- привязки точек и выводов от угла и от пола, мм
- мебель и приборы — фасад по расстановке (условно)
- зеркало: марка Д, крест — центр, Н — высота центра, мм
- стены и перекрытия в сечении
- окраска: тон — цвет по коду производителя (условно)
- О1 — марка отделки по реестру отделки альбома
- А — марка развёртки: буква стены, стрелка — взгляд

Ведомость отделки (на листе)

Марка	Поверхность	Материал, изделие	Цвет, код	Кол.
О1	стены	окраска, Farrow & Ball Modern Emulsion, матовая, подготовка Q3	Farrow & Ball No. 291 «School House White — тёплый меловой белый»	5,7 м²
О3	плинтус	плинтус МДФ, h 83 мм, Ultrawood Base 5340, ЛДФ под окраску, 83×15 мм, 2440 мм (арт. LDF-BASE-5340)	Farrow & Ball No. 291 «School House White — тёплый меловой белый»	1,2 м
О4	потолок	окраска, Tikkurila Anti-Reflex 2, глубокоматовая, подготовка Q3	NCS S 0502-Y «Белый с лёгкой желтизной»	12,9 м²

Допущения и предложения на листе

Основа листа: размеры сняты со скана обмерного плана KV design (см): часть подписей не читается, помещения выровнены по читаемым размерам; контрольный обмер не выполнен (К-1); высота потолка 2650 мм принята по отметкам обмера (Н = 2,50…2,66 м, ригель 2,28 м) — уточнить при обмере (К-2); толщины стен 300 / 120 мм приняты, межквартирная стена и колонны — по скану, не замерены (К-1); разрешённая мощность 15 кВт принята по типовым ТУ; при объединении двух квартир — переоформление ТУ (К-4); подрайон климата не задан — принят не северный (жилые от 2,5 м) (К-8).

Знак «**» — предложение проектировщика, заказчиком не утверждено (согласовать с заказчиком): Р17 — высота 1700 мм выше нормы 1 м (ПУЭ 6.6.30) по назначению: питание слаботочного щита ЩС, рядом со щитом на его высоте; ЩС — щит слаботочный: место и состав.

См. лист открытых вопросов (лист 6, записи К-1, К-2, К-4, К-8).

Примечания

1. Развёртки — вид на стену изнутри помещения, по часовой стрелке; расположение — на схеме листа и на листе 79; размеры — в мм по чистовым поверхностям; отметки — в м от ±0,000; высоты Н — от чистого пола помещения до оси изделия, у декора — до центра.
2. Красная цепочка — привязки электроточек и выводов по осям от угла чистовых стен; высота Н — у знака, от чистого пола до оси; высоты мебели, проёмов и границ отделки — колонкой отметок слева. Стена с 5 и более точками или с мелкими звеньями привязок показана двумя видами: архитектурная развёртка (мебель, отделка, проёмы, высоты) и вид «Привязки» на отдельном листе — точки и выводы с марками, одна цепочка по осям и таблица привязок (каждая точка — строка).
3. У знака электроточки: марка (Р — розетка, S — выключатель, Св — светильник, ЭВ — вывод кабеля), ×N — число постов в рамке, гр. — группа щита, Н — высота оси от чистого пола, мм; группы по клавишам выключателя — на листе выключателей.
4. Схема мебели, приборов и декора не является технической документацией для производства мебели; габариты — по паспортам изделий.
5. Картины и зеркала крепить к основанию по паспорту изделия (закладные и анкеры — в перечне скрытых работ); крест — ось центра предмета.

1000 мм · печать 1:1

Изм.	Кол.уч	Лист	№ док.	Подп.	Дата
Разраб.		Кырлан А.С.			04.11.26
Пров.					
ГИП					
Н. контр.					
Утв.					

ГД-2026-009-АИ

Квартира 103 м²

Общая площадь 100,72* м² · * размеры со скана, не замерены (реестр — л. 6, 7, К-1)

Дизайн-проект интерьера

Стадия	Лист	Листов
РП	89	120

Развёртка стены Б. Прихожая-холл (пом. 4)

М 1:20

Кырлан Александр Сергеевич


выпуск 04.11.2026 № 20cec94f32 · стр. 98 из 130

Развёртка стены В. Прихожая-холл (пом. 4)

Прихожая-холл (пом. 4) · вид изнутри помещения · размеры в мм, отметки в м

ПРЕДВАРИТЕЛЬНО · не для производства работ · открыто пунктов: 8 (реестр — л. 6, 7)

Развёртка стены В

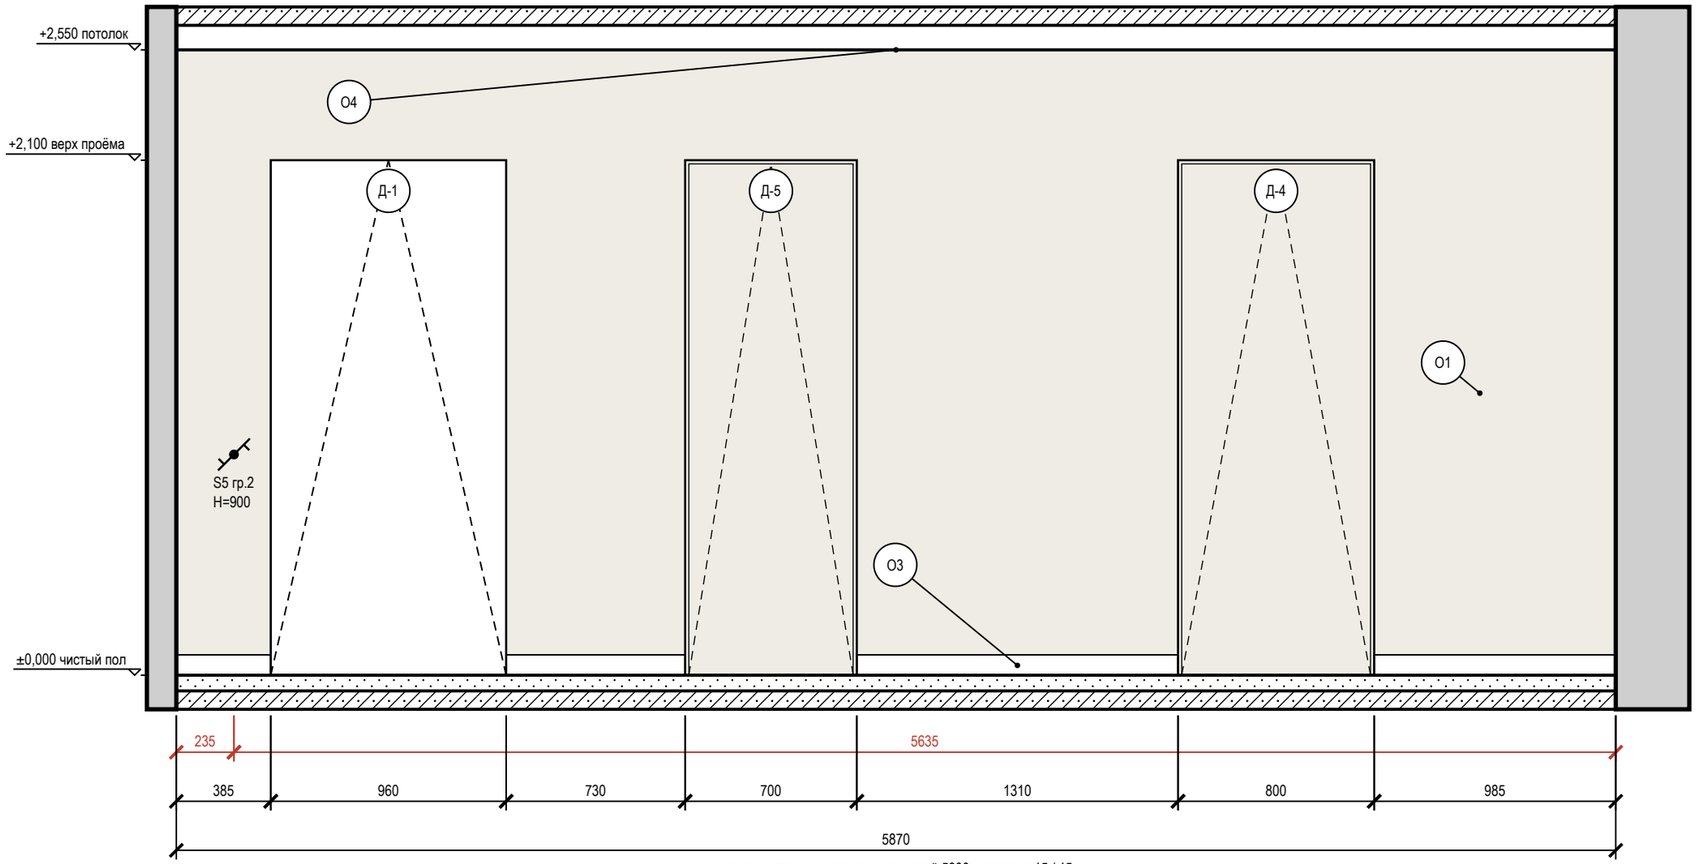


между чистовыми гранями: черновой 5900 − отделка 15 / 15

Условные обозначения

- выключатель одноклавишный
- выключатель с проходной или перекрёстной клавишей (обратный флажок); тип клавиши — в подписи
- привязки точек и выводов от угла и от пола, мм
- мебель и приборы — фасад по расстановке (условно)
- дверь скрытого монтажа: полотно в плоскости стены (узел — на листе узлов)
- дверной проём; марка двери — в кружке
- стены и перекрытия в сечении
- окраска: тон — цвет по коду производителя (условно)
- О1 — марка отделки по реестру отделки альбома
- А — марка развёртки: буква стены, стрелка — взгляд

Схема развёрток (М 1:100)

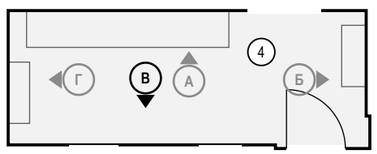

Ведомость отделки (на листе)

Марка	Поверхность	Материал, изделие	Цвет, код	Кол.
О1	стены	окраска, Farrow & Ball Modern Emulsion, матовая, подготовка Q3	Farrow & Ball No. 291 «School House White тёплый меловой белый»	9,8 м²
О3	плинтус	плинтус МДФ, h 83 мм, Ultrawood Base 5340, ЛДФ под окраску, 83×15 мм, 2440 мм (арт. LDF-BASE-5340)	Farrow & Ball No. 291 «School House White тёплый меловой белый»	3,4 м
О4	потолок	окраска, Tikkurila Anti-Reflex 2, глубокоматовая, подготовка Q3	NCS S 0502-Y «Белый с лёгкой желтизной»	12,9 м²

Допущения и предложения на листе

Основа листа: размеры сняты со скана обмерного плана KV design (см): часть подписей не читается, помещения выровнены по читаемым размерам; контрольный обмер не выполнен (К-1); высота потолка 2650 мм принята по отметкам обмера (Н = 2,50…2,66 м, ригель 2,28 м) — уточнить при обмере (К-2); толщины стен 300 / 120 мм приняты, межквартирная стена и колонны — по скану, не замерены (К-1); разрешённая мощность 15 кВт принята по типовым ТУ; при объединении двух квартир — переоформление ТУ (К-4); подрайон климата не задан — принят не северный (жилые от 2,5 м) (К-8).
См. лист открытых вопросов (лист 6, записи К-1, К-2, К-4, К-8).

Примечания

1. Развёртки — вид на стену изнутри помещения, по часовой стрелке; расположение — на схеме листа и на листе 79; размеры — в мм по чистовым поверхностям; отметки — в м от ±0,000; высоты Н — от чистого пола помещения до оси изделия, у декора — до центра.
2. Красная цепочка — привязки электроточек и выводов по осям от угла чистовых стен; высота Н — у знака, от чистого пола до оси; высоты мебели, проёмов и границ отделки — колонкой отметок слева. Стена с 5 и более точками или с мелкими звеньями привязок показана двумя видами: архитектурная развёртка (мебель, отделка, проёмы, высоты) и вид «Привязки» на отдельном листе — точки и выводы с марками, одна цепочка по осям и таблица привязок (каждая точка — строка).
3. У знака электроточки: марка (Р — розетка, S — выключатель, Св — светильник, ЭВ — вывод кабеля), ×N — число постов в рамке, гр. — группа щита, Н — высота оси от чистого пола, мм; группы по клавишам выключателя — на листе выключателей.
4. Схема мебели, приборов и декора не является технической документацией для производства мебели; габариты — по паспортам изделий.
5. Двери скрытого монтажа — полотно в плоскости стены, отделка стены по полотну, плинтус прерывается у короба (узел — на листе узлов).

1000 мм · печать 1:1

Изм.	Кол.уч	Лист	№ док.	Подп.	Дата
Разраб.		Кырлан А.С.			04.11.26
Пров.					
ГИП					
Н. контр.					
Утв.					

ГД-2026-009-АИ

Квартира 103 м²

Общая площадь 100,72* м² · * размеры со скана, не замерены (реестр — л. 6, 7, К-1)

Дизайн-проект интерьера

Стадия	Лист	Листов
РП	90	120

Развёртка стены В. Прихожая-холл (пом. 4)

М 1:25

Кырлан Александр Сергеевич

выпуск 04.11.2026 № 20cec94f32 · стр. 99 из 130

Развёртка стены Г. Прихожая-холл (пом. 4)

Прихожая-холл (пом. 4) · вид изнутри помещения · размеры в мм, отметки в м

Развёртка стены Г


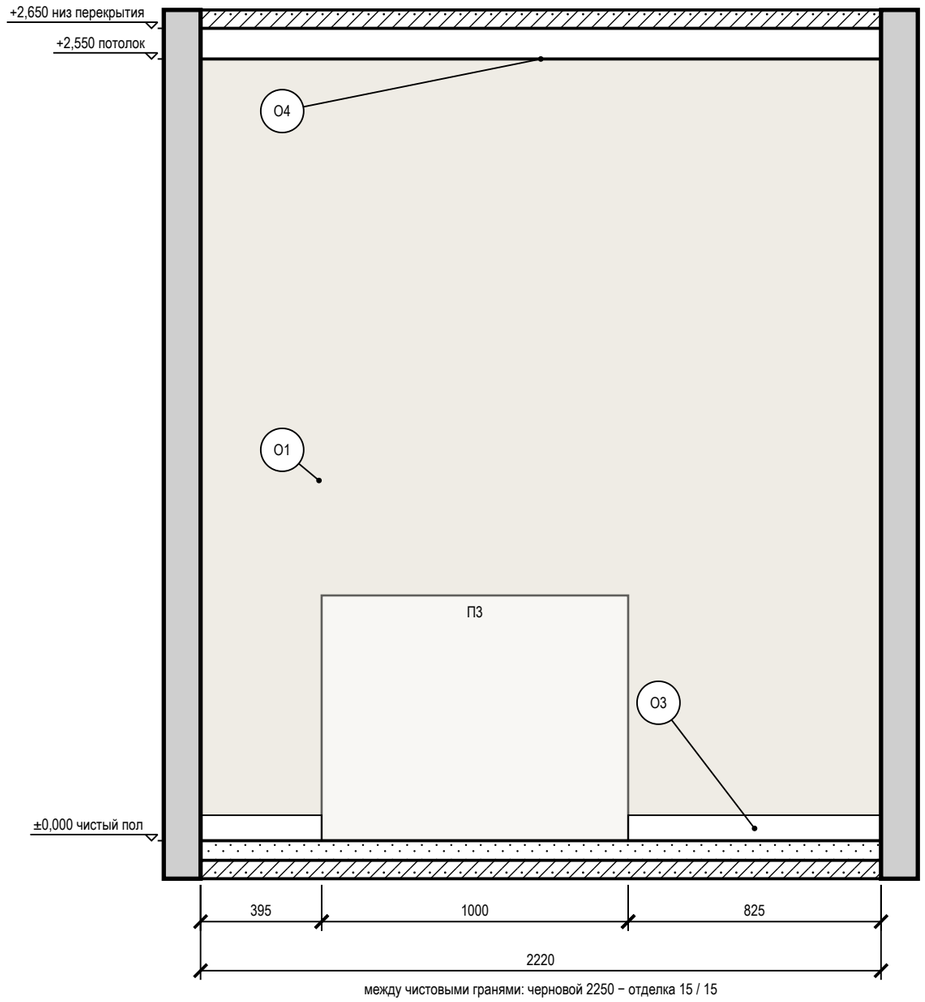


Схема развёрток (М 1:100)

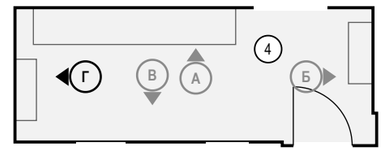

Условные обозначения

- мебель и приборы — фасад по расстановке (условно)
- стены и перекрытия в сечении
- окраска: тон — цвет по коду производителя (условно)
- О1 — марка отделки по реестру отделки альбома
- А — марка развёртки: буква стены, стрелка — взгляд

Ведомость отделки (на листе)

Марка	Поверхность	Материал, изделие	Цвет, код	Кол.
О1	стены	окраска, Farrow & Ball Modern Emulsion, матовая, подготовка Q3	Farrow & Ball No. 291 «School House White — тёплый меловой белый»	5,7 м²
О3	плинтус	плинтус МДФ, h 83 мм, Ultrawood Base 5340, ЛДФ под окраску, 83×15 мм, 2440 мм (арт. LDF-BASE-5340)	Farrow & Ball No. 291 «School House White — тёплый меловой белый»	1,2 м
О4	потолок	окраска, Tikkurila Anti-Reflex 2, глубокоматовая, подготовка Q3	NCS S 0502-Y «Белый с лёгкой желтизной»	12,9 м²

Примечания

1. Развёртки — вид на стену изнутри помещения, по часовой стрелке; расположение — на схеме листа и на листе 79; размеры — в мм по чистовым поверхностям; отметки — в м от ±0,000; высоты Н — от чистого пола помещения до оси изделия, у декора — до центра.
2. Схема мебели, приборов и декора не является технической документацией для производства мебели; габариты — по паспортам изделий.

Допущения и предложения на листе

Основа листа: размеры сняты со скана обмерного плана KV design (см): часть подписей не читается, помещения выровнены по читаемым размерам; контрольный обмер не выполнен (К-1); высота потолка 2650 мм принята по отметкам обмера (Н = 2,50…2,66 м, ригель 2,28 м) — уточнить при обмере (К-2); толщины стен 300 / 120 мм приняты, межквартирная стена и колонны — по скану, не замерены (К-1); разрешённая мощность 15 кВт принята по типовым ТУ; при объединении двух квартир — переоформление ТУ (К-4); подрайон климата не задан — принят не северный (жилые от 2,5 м) (К-8).
См. лист открытых вопросов (лист 6, записи К-1, К-2, К-4, К-8).

1000 мм · печать 1:1

Изм.	Кол.уч	Лист	№ док.	Подп.	Дата
Разраб.		Кырлан А.С.			04.11.26
Пров.					
ГИП					
Н. контр.					
Утв.					

ГД-2026-009-АИ

Квартира 103 м²

Общая площадь 100,72* м² · * размеры со скана, не замерены (реестр — л. 6, 7, К-1)

Дизайн-проект интерьера

Стадия	Лист	Листов
РП	91	120

Развёртка стены Г. Прихожая-холл (пом. 4)

М 1:20


Кырлан Александр Сергеевич

Развёртки стен Б, В. Кухня (пом. 5), кухонный фронт

Кухня (пом. 5) · вид изнутри помещения · размеры в мм, отметки в м


ПРЕДВАРИТЕЛЬНО · не для производства работ · открыто пунктов: 8 (реестр — л. 6, 7)

Развёртка стены Б

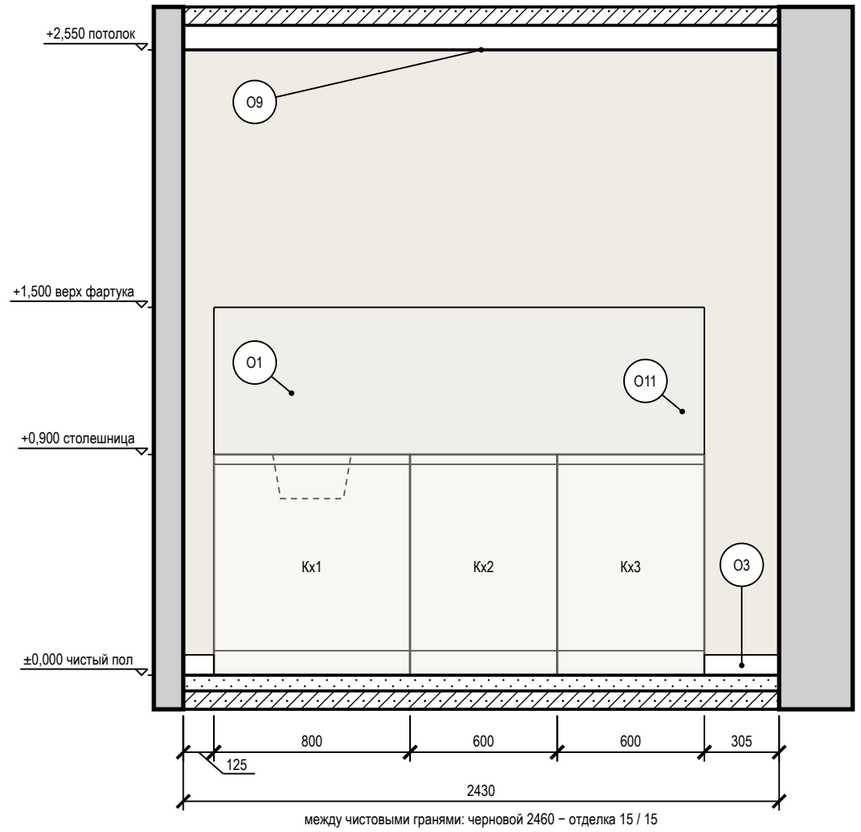


между чистовыми гранями: черновой 2460 − отделка 15 / 15

Развёртка стены В

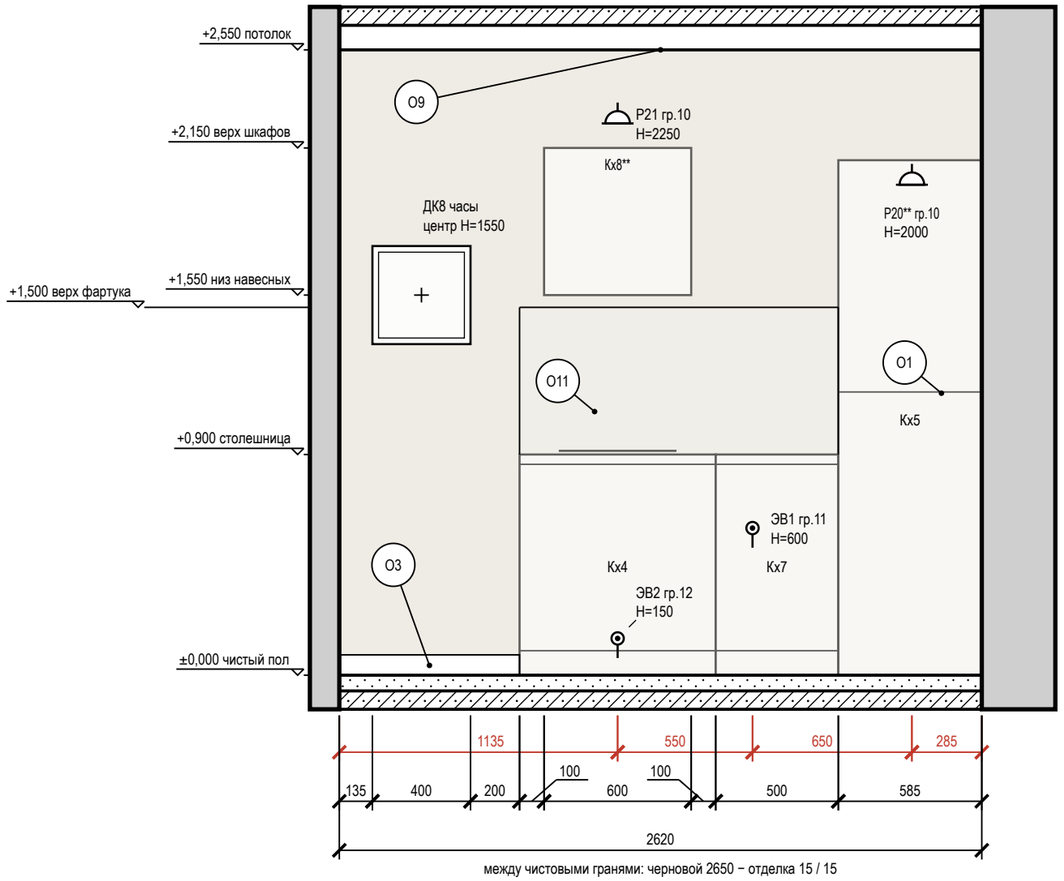

между чистовыми гранями: черновой 2650 − отделка 15 / 15

Схема развёрток (М 1:100)

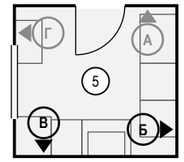

Условные обозначения

- розетка с заземляющим контактом; у знака — марка, ×N постов в рамке, гр. — группа щита, Н — высота оси, мм
- вывод кабеля для подключения прибора (без розетки), марка ЭВ
- привязки точек и выводов от угла и от пола, мм
- мебель и приборы — фасад по расстановке (условно)
- картина (декор): марка Д, крест — центр, Н — высота центра, мм
- стены и перекрытия в сечении
- плитка: сетка швов по формату, ▲ — ось старта
- окраска: тон — цвет по коду производителя (условно)
- О1 — марка отделки по реестру отделки альбома
- А — марка развёртки: буква стены, стрелка — взгляд

Допущения и предложения на листе

Основа листа: размеры сняты со скана обмерного плана KV design (см): часть подписей не читается, помещения выровнены по читаемым размерам; контрольный обмер не выполнен (К-1); высота потолка 2650 мм принята по отметкам обмера (Н = 2,50…2,66 м, ригель 2,28 м) — уточнить при обмере (К-2); толщины стен 300 / 120 мм приняты, межквартирная стена и колонны — по скану, не замерены (К-1); разрешённая мощность 15 кВт принята по типовым ТУ; при объединении двух квартир — переоформление ТУ (К-4); подрайон климата не задан — принят не северный (жилые от 2,5 м) (К-8).

Знак «**» — предложение проектировщика, заказчиком не утверждено (согласовать с заказчиком): Кх8 — над индукционной панелью Кх4 нужна вытяжка: в составе кухни её не было, розетка вытяжки образца висела без потребителя; Р20 — высота 2000 мм выше нормы 1 м (ПУЭ 6.6.30) по назначению: розетка встроенного прибора — в колонне Кх5 над нишей, в антресоли за съёмной панелью.

См. лист открытых вопросов (лист 6, записи К-1, К-2, К-4, К-8).

Примечания

1. Развёртки — вид на стену изнутри помещения, по часовой стрелке; расположение — на схеме листа и на листе 79; размеры — в мм по чистовым поверхностям; отметки — в м от ±0,000; высоты Н — от чистого пола помещения до оси изделия, у декора — до центра.
2. Красная цепочка — привязки электроточек и выводов по осям от угла чистовых стен; высота Н — у знака, от чистого пола до оси; высоты мебели, проёмов и границ отделки — колонкой отметок слева. Стена с 5 и более точками или с мелкими звеньями привязок показана двумя видами: архитектурная развёртка (мебель, отделка, проёмы, высоты) и вид «Привязки» на отдельном листе — точки и выводы с марками, одна цепочка по осям и таблица привязок (каждая точка — строка).
3. Стена Б показана двумя видами: здесь — архитектурная развёртка (мебель, отделка, проёмы, высоты), электроточки и выводы ВК с привязками и таблицей — на листе 93 («Привязки»).
4. У знака электроточки: марка (Р — розетка, S — выключатель, Св — светильник, ЭВ — вывод кабеля), ×N — число постов в рамке, гр. — группа щита, Н — высота оси от чистого пола, мм; группы по клавишам выключателя — на листе выключателей.
5. Схема мебели, приборов и декора не является технической документацией для производства мебели; габариты — по паспортам изделий.
6. Картины и зеркала крепить к основанию по паспорту изделия (закладные и анкеры — в перечне скрытых работ); крест — ось центра предмета.
7. Выводы кухонной техники — по утверждённому проекту кухни: привязки выводов даются от осей модулей гарнитура.

1000 мм · печать 1:1

Изм.	Кол.уч	Лист	№ док.	Подп.	Дата
Разраб.		Кырлан А.С.			04.11.26
Пров.					
ГИП					
Н. контр.					
Утв.					

ГД-2026-009-АИ

Квартира 103 м²

Общая площадь 100,72* м² · * размеры со скана, не замерены (реестр — л. 6, 7, К-1)

Дизайн-проект интерьера

Стадия	Лист	Листов
РП	92	120

Развёртки стен Б, В. Кухня (пом. 5), кухонный фронт

М 1:25

Кырлан Александр Сергеевич

выпуск 04.11.2026 № 20cec94f32 · стр. 101 из 130

Привязки электроточек и выводов ВК, стена Б. Кухня (пом. 5)

Кухня (пом. 5) · вид изнутри помещения · привязки в мм, отметки в м · к развёртке на листе 92

ПРЕДВАРИТЕЛЬНО · не для производства работ · открыто пунктов: 8 (реестр — л. 6, 7)

Развёртка стены Б: электроточки и выводы

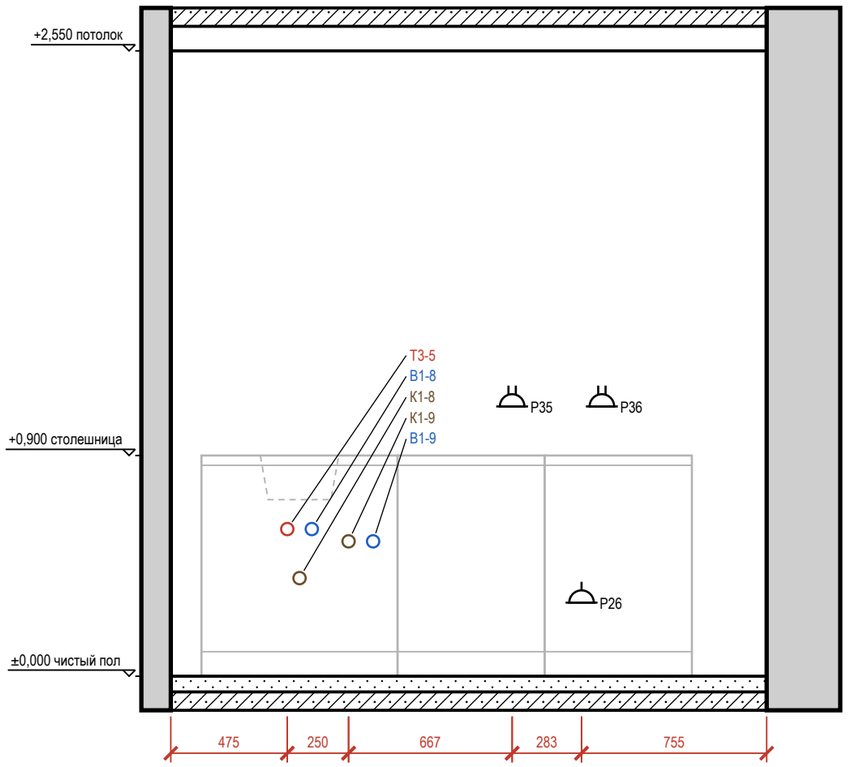



Таблица привязок электроточек и выводов

Марка	Назначение	От угла, мм	Н от пола, мм	Примечание
Т3-5	горячая вода — мойка кухонная	475	600*	межос. 100
К1-8	канализация — мойка кухонная	525	400*	Ø50
В1-8	холодная вода — мойка кухонная	575	600*	межос. 100
К1-9	канализация — посудомоечная машина	725	550*	Ø40; слив ПММ в шкафу мойки
В1-9	холодная вода — посудомоечная машина	825	550*	кран ПММ в шкафу мойки
Р35	розетка: фартук	1392	1100	рамка 2 поста, гр. 9
Р26	розетка: посудомоечная машина — в соседнем модуле, за ящиком	1675	300	гр. 13
Р36	розетка: фартук	1758	1100	рамка 2 поста, гр. 9

Условные обозначения

- розетка с заземляющим контактом; у знака — марка, ×N постов в рамке, гр. — группа щита, Н — высота оси, мм
- вывод В1 (код — в ведомости привязок)
- вывод Т3 (код — в ведомости привязок)
- вывод К1 (код — в ведомости привязок)
- привязки точек и выводов от угла и от пола, мм
- марка развёртки: буква стены, стрелка — взгляд

Схема развёрток (М 1:100)

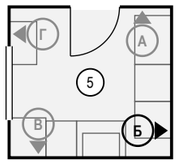

Примечания

1. Вид «Привязки» стены Б — электроточки и выводы ВК; архитектурная развёртка (мебель, отделка, проёмы, высоты) — на листе 92, расположение — на листе 79. Мебель и приборы — подложкой для ориентира; их марки и обозначения мебели, проёмов и стен — там же.
2. Привязки — в мм: по горизонтали от левого чистового угла стены до оси изделия, Н — от чистого пола до оси; все точки — в таблице привязок. Красная цепочка — привязки по осям; точки ближе 150 мм одна к другой в цепочку не дробятся — их привязки только в таблице.
3. У знака — марка электроточки (Р — розетка, S — выключатель, Св — светильник, ЭВ — вывод кабеля); посты в рамке и группа щита — в графе «Примечание»; группы по клавишам выключателя — на листе выключателей.
4. Коды выводов ВК: В1 — холодная вода, Т3 — горячая вода, К1 — канализация; номер после дефиса — номер вывода на листе выводов сантехники; * — высота принята по типовой практике монтажа, окончательно — по паспорту прибора.
5. Выводы кухонной техники — по утверждённому проекту кухни: привязки выводов даются от осей модулей гарнитура.

Допущения и предложения на листе

Основа листа: размеры сняты со скана обмерного плана KV design (см): часть подписей не читается, помещения выровнены по читаемым размерам; контрольный обмер не выполнен (К-1); высота потолка 2650 мм принята по отметкам обмера (Н = 2,50…2,66 м, ригель 2,28 м) — уточнить при обмере (К-2); толщины стен 300 / 120 мм приняты, межквартирная стена и колонны — по скану, не замерены (К-1); разрешённая мощность 15 кВт принята по типовым ТУ; при объединении двух квартир — переоформление ТУ (К-4); подрайон климата не задан — принят не северный (жилые от 2,5 м) (К-8).

См. лист открытых вопросов (лист 6, записи К-1, К-2, К-4, К-8).

1000 мм · печать 1:1

Изм.	Кол.уч	Лист	№ док.	Подп.	Дата
Разраб.		Кырлан А.С.			04.11.26
Пров.					
ГИП					
Н. контр.					
Утв.					

ГД-2026-009-АИ

Квартира 103 м²

Общая площадь 100,72* м² · * размеры со скана, не замерены (реестр — л. 6, 7, К-1)

Дизайн-проект интерьера	Стадия	Лист	Листов
	РП	93	120

Привязки электроточек и выводов ВК, стена Б. Кухня (пом. 5)

М 1:25

Кырлан Александр Сергеевич


выпуск 04.11.2026 № 20cec94f32 · стр. 102 из 130

Развёртки стен А, Г. Кухня (пом. 5)

Кухня (пом. 5) · вид изнутри помещения · размеры в мм, отметки в м


ПРЕДВАРИТЕЛЬНО · не для производства работ · открыто пунктов: 8 (реестр — л. 6, 7)

Развёртка стены А

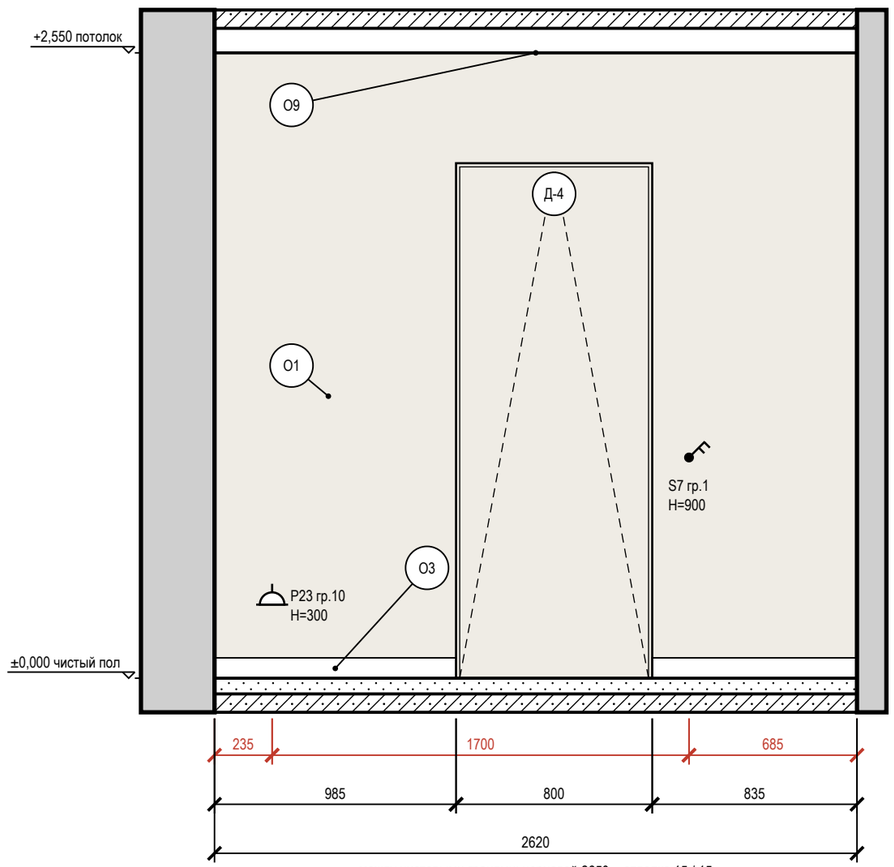


между чистовыми гранями: черновой 2650 − отделка 15 / 15

Развёртка стены Г

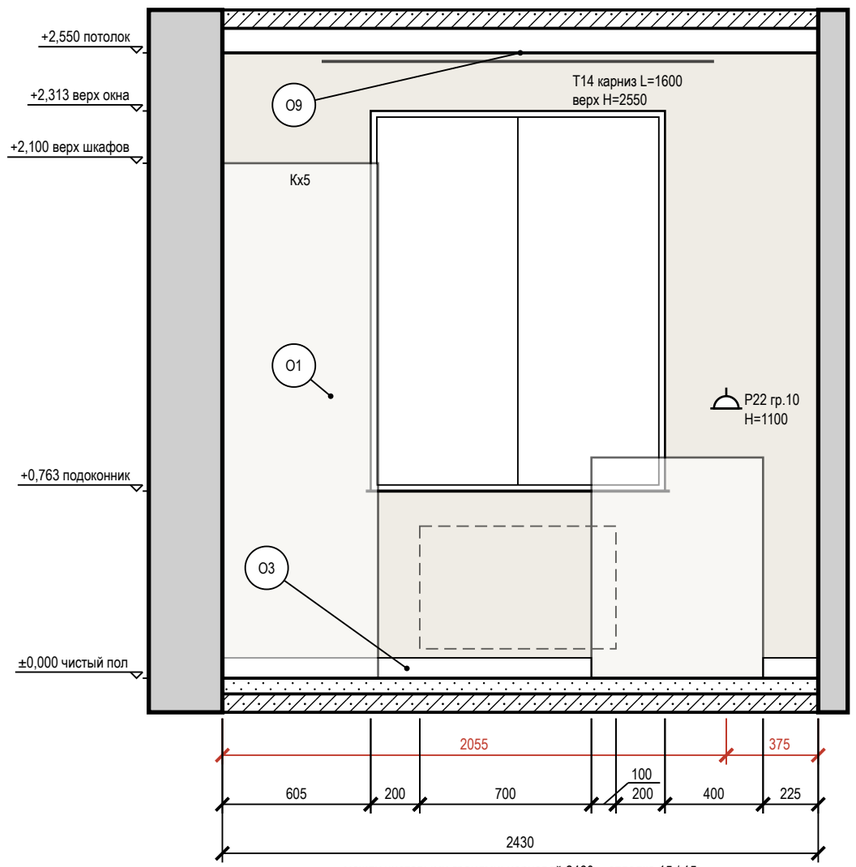

между чистовыми гранями: черновой 2460 − отделка 15 / 15

Схема развёрток (М 1:100)

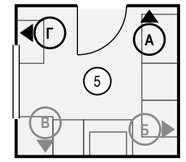

Условные обозначения

- розетка с заземляющим контактом; у знака — марка, ×N постов в рамке, гр. — группа щита, H — высота оси, мм
- выключатель одноклавишный
- выключатель двухклавишный (флажков — по числу клавиш)
- привязки точек и выводов от угла и от пола, мм
- мебель и приборы — фасад по расстановке (условно)
- карниз (шина) и шторы в собранном виде: марка T, длина L, верх H
- дверь скрытого монтажа: полотно в плоскости стены (узел — на листе узлов)
- окно: проём, рама, подоконник
- радиатор отопления; марка — по плану отопления
- стены и перекрытия в сечении
- окраска: тон — цвет по коду производителя (условно)
- О1 — марка отделки по реестру отделки альбома
- А — марка развёртки: буква стены, стрелка — взгляд

Допущения и предложения на листе

Основа листа: размеры сняты со скана обмерного плана KV design (см): часть подписей не читается, помещения выровнены по читаемым размерам; контрольный обмер не выполнен (К-1); высота потолка 2650 мм принята по отметкам обмера (H = 2,50…2,66 м, ригель 2,28 м) — уточнить при обмере (К-2); толщины стен 300 / 120 мм приняты, межквартирная стена и колонны — по скану, не замерены (К-1); разрешённая мощность 15 кВт принята по типовым ТУ; при объединении двух квартир — переоформление ТУ (К-4); подрайон климата не задан — принят не северный (жилые от 2,5 м) (К-8).

См. лист открытых вопросов (лист 6, записи К-1, К-2, К-4, К-8).

Примечания

1. Развёртки — вид на стену изнутри помещения, по часовой стрелке; расположение — на схеме листа и на листе 79; размеры — в мм по чистовым поверхностям; отметки — в м от ±0,000; высоты H — от чистого пола помещения до оси изделия, у декора — до центра.
2. Красная цепочка — привязки электроточек и выводов по осям от угла чистовых стен; высота H — у знака, от чистого пола до оси; высоты мебели, проёмов и границ отделки — колонкой отметок слева. Стена с 5 и более точками или с мелкими звеньями привязок показана двумя видами: архитектурная развёртка (мебель, отделка, проёмы, высоты) и вид «Привязки» на отдельном листе — точки и выводы с марками, одна цепочка по осям и таблица привязок (каждая точка — строка).
3. У знака электроточки: марка (Р — розетка, S — выключатель, Св — светильник, ЭВ — вывод кабеля), ×N — число постов в рамке, гр. — группа щита, H — высота оси от чистого пола, мм; группы по клавишам выключателя — на листе выключателей.
4. Схема мебели, приборов и декора не является технической документацией для производства мебели; габариты — по паспортам изделий.
5. Карнизы (шины) — по ведомости текстиля декоратора: длина L и верх H на развёртке — те же числа, что в ведомости; крепление — до окраски потолка.
6. Двери скрытого монтажа — полотно в плоскости стены, отделка стены по полотну, плинтус прерывается у короба (узел — на листе узлов).

1000 мм · печать 1:1

Изм.	Кол.уч	Лист	№ док.	Подп.	Дата
Разраб.		Кырлан А.С.			04.11.26
Пров.					
ГИП					
Н. контр.					
Утв.					

ГД-2026-009-АИ

Квартира 103 м²

Общая площадь 100,72* м² · * размеры со скана, не замерены (реестр — л. 6, 7, К-1)

Дизайн-проект интерьера	Стадия	Лист	Листов
	РП	94	120

Развёртки стен А, Г. Кухня (пом. 5)

М 1:25

Кырлан Александр Сергеевич


выпуск 04.11.2026 № 20cec94f32 · стр. 103 из 130

Развёртки стен А, Б, В. Ванная (пом. 6)

Ванная (пом. 6) · вид изнутри помещения · размеры в мм, отметки в м


ПРЕДВАРИТЕЛЬНО · не для производства работ · открыто пунктов: 8 (реестр — л. 6, 7)

Развёртка стены А

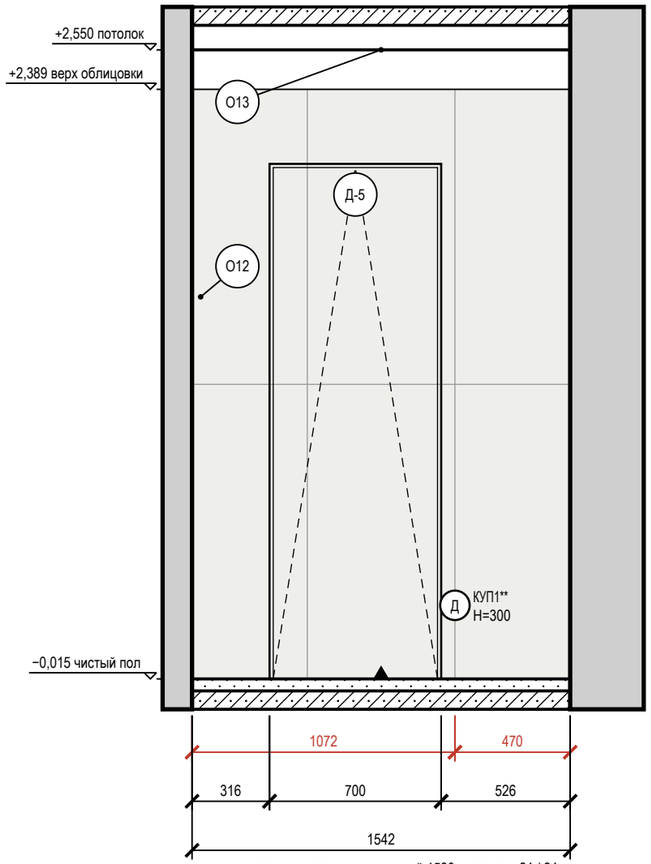


между чистовыми гранями: черновой 1590 − отделка 24 / 24

Развёртка стены Б

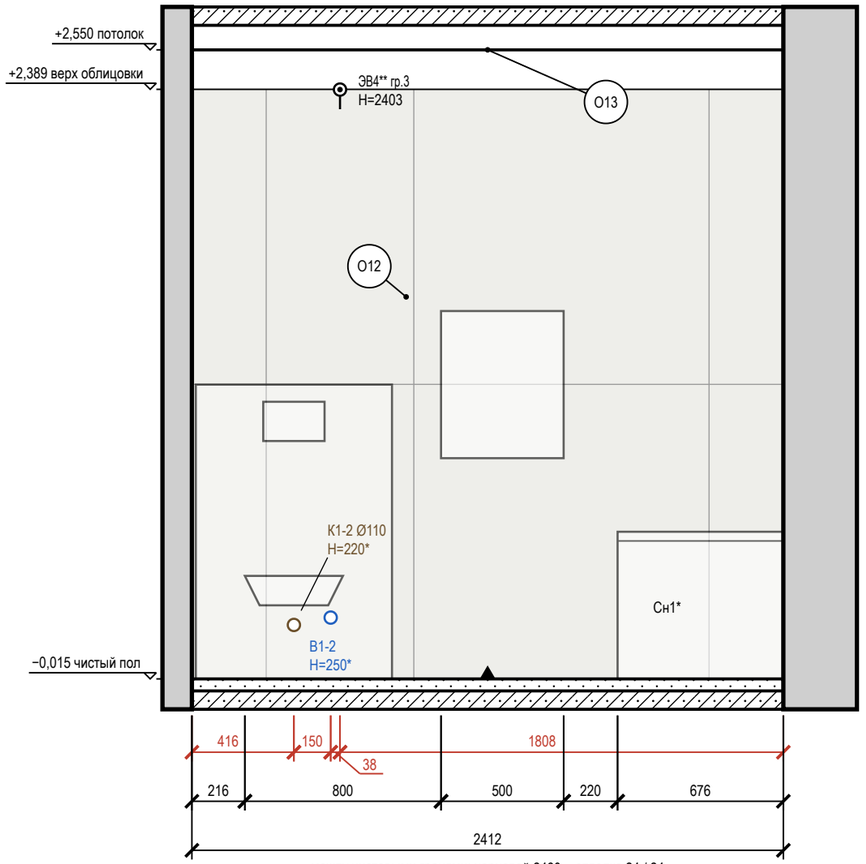


между чистовыми гранями: черновой 2460 − отделка 24 / 24

Развёртка стены В

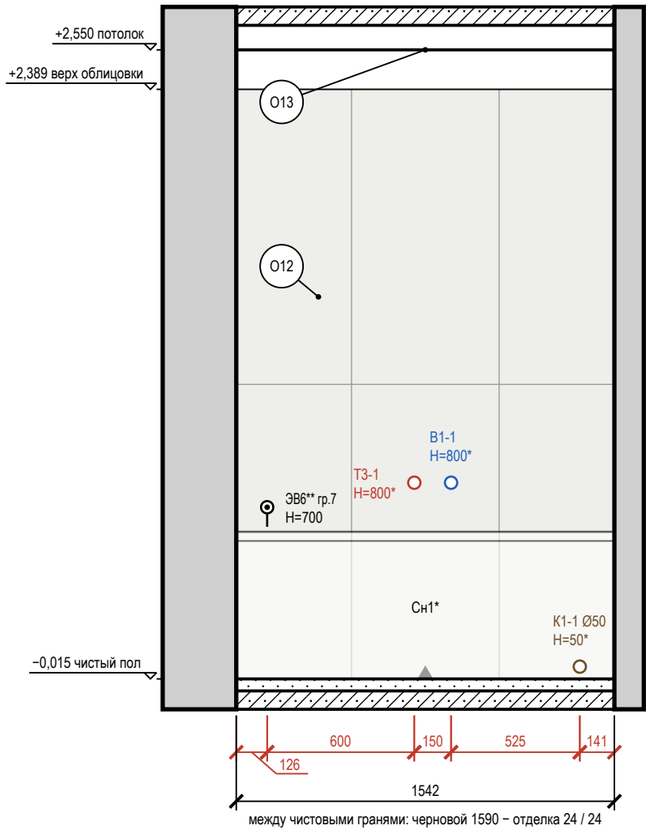

между чистовыми гранями: черновой 1590 − отделка 24 / 24

Схема развёрток (М 1:100)

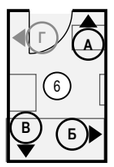

Условные обозначения

- вывод кабеля для подключения прибора (без розетки), марка ЭВ
- вывод В1 (код — в ведомости привязок)
- вывод Т3 (код — в ведомости привязок)
- вывод К1 (код — в ведомости привязок)
- привязки точек и выводов от угла и от пола, мм
- мебель и приборы — фасад по расстановке (условно)
- дверь скрытого монтажа: полотно в плоскости стены (узел — на листе узлов)
- стены и перекрытия в сечении
- плитка: сетка швов по формату, ▲ — ось старта
- О1 — марка отделки по реестру отделки альбома
- А — марка развёртки: буква стены, стрелка — взгляд

Допущения и предложения на листе. Знак «**» предложено (согласовать). См. лист открытых вопросов (лист 6).

Ведомость отделки (на листе)

Марка	Поверхность	Материал, изделие	Цвет, код	Кол.
О12	стены	облицовка плиткой, Atlas Concorde Marvel Travertine, 600×1200×9 мм, A8UZ, затирка CG2WA	Atlas Concorde A8UZ «Marvel Travertine»	11,7 м²
О13	потолок	окраска, Tikkurila Luja 7, матовая, подготовка Q3	NCS S 0502-Y «Белый с лёгкой желтизной»	3,9 м²

Примечания

1. Развёртки — вид на стену изнутри помещения, по часовой стрелке; расположение — на схеме листа и на листе 79; размеры — в мм по чистовым поверхностям; отметки — в м от ±0,000; высоты Н — от чистого пола помещения до оси изделия, у декора — до центра.
2. Красная цепочка — привязки электроточек и выводов по осям от угла чистовых стен; высота Н — у знака, от чистого пола до оси; высоты мебели, проёмов и границ отделки — колонкой отметок слева. Стена с 5 и более точками или с мелкими звеньями привязок показана двумя видами: архитектурная развёртка (мебель, отделка, проёмы, высоты) и вид «Привязки» на отдельном листе — точки и выводы с марками, одна цепочка по осям и таблица привязок (каждая точка — строка).
3. У знака электроточки: марка (Р — розетка, S — выключатель, Св — светильник, ЭВ — вывод кабеля), ×N — число постов в рамке, гр. — группа щита, Н — высота оси от чистого пола, мм; группы по клавишам выключателя — на листе выключателей.
4. Схема мебели, приборов и декора не является технической документацией для производства мебели; габариты — по паспортам изделий (* — высота не задана в проекте, показана по типовому изделию).
5. Выводы ВК — коды и высоты по листу выводов сантехники; * — высота принята по типовой практике монтажа, окончательно — по паспорту прибора.
6. Облицовка — по сетке швов 2 мм, раскладка от оси стены (треугольник у пола), целые ряды от пола; подрезки — по листу раскладки плитки.
7. Гидроизоляция в 2 слоя, заход на стены 200 мм; над ванной — до 2000 и 300 мм за борт — до облицовки, с актом скрытых работ и тестом проливом (узел — на листе узлов).
8. Двери скрытого монтажа — полотно в плоскости стены, отделка стены по полотну, плинтус прерывается у короба (узел — на листе узлов).

1000 мм · печать 1:1

Изм.	Кол.уч	Лист	№ док.	Подп.	Дата
Разраб.		Кырлан А.С.			04.11.26
Пров.					
ГИП					
Н. контр.					
Утв.					

ГД-2026-009-АИ

Квартира 103 м²

Общая площадь 100,72* м² · * размеры со скана, не замерены (реестр — л. 6, 7, К-1)

Дизайн-проект интерьера

Стадия	Лист	Листов
РП	95	120

Развёртки стен А, Б, В. Ванная (пом. 6)

М 1:25


Кырлан Александр Сергеевич

выпуск 04.11.2026 № 20cec94f32 · стр. 104 из 130

Развёртка стены Г. Ванная (пом. 6)


Ванная (пом. 6) · вид изнутри помещения · размеры в мм, отметки в м

Развёртка стены Г

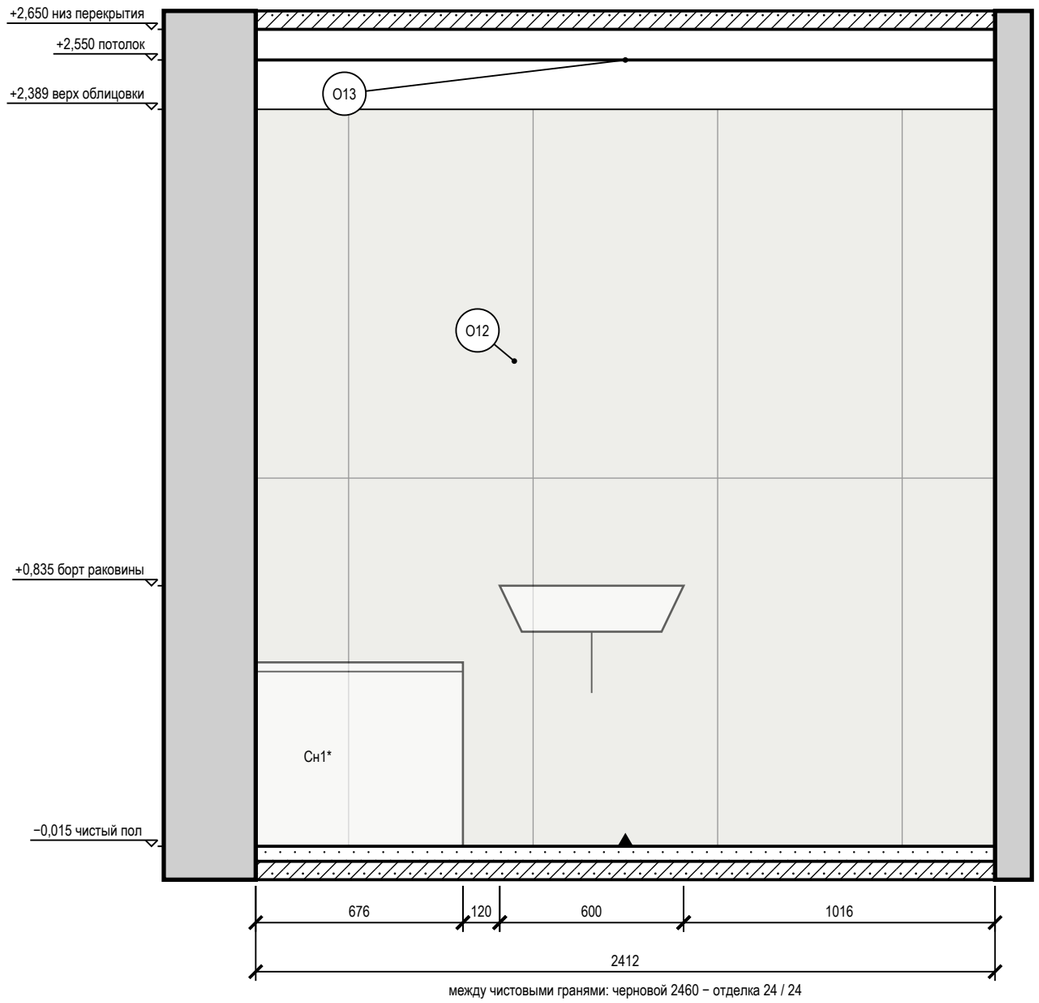

между чистовыми гранями: черновой 2460 − отделка 24 / 24

Схема развёрток (М 1:100)

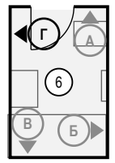

Условные обозначения

- мебель и приборы — фасад по расстановке (условно)
- стены и перекрытия в сечении
- плитка: сетка швов по формату, ▲ — ось старта
- О1 — марка отделки по реестру отделки альбома
- А — марка развёртки: буква стены, стрелка — взгляд

Ведомость отделки (на листе)

Марка	Поверхность	Материал, изделие	Цвет, код	Кол.
О12	стены	облицовка плиткой, Atlas Concorde Marvel Travertine, 600×1200×9 мм, A8UZ, затирка CG2WA	Atlas Concorde A8UZ «Marvel Travertine»	5,8 м²
О13	потолок	окраска, Tikkurila Luja 7, матовая, подготовка Q3	NCS S 0502-Y «Белый с лёгкой желтизной»	3,9 м²

Допущения и предложения на листе

Основа листа: размеры сняты со скана обмерного плана KV design (см): часть подписей не читается, помещения выровнены по читаемым размерам; контрольный обмер не выполнен (К-1); высота потолка 2650 мм принята по отметкам обмера (Н = 2,50…2,66 м, ригель 2,28 м) — уточнить при обмере (К-2); толщины стен 300 / 120 мм приняты, межквартирная стена и колонны — по скану, не замерены (К-1); разрешённая мощность 15 кВт принята по типовым ТУ; при объединении двух квартир — переоформление ТУ (К-4); подрайон климата не задан — принят не северный (жилые от 2,5 м) (К-8).

См. лист открытых вопросов (лист 6, записи К-1, К-2, К-4, К-8).

Примечания

1. Развёртки — вид на стену изнутри помещения, по часовой стрелке; расположение — на схеме листа и на листе 79; размеры — в мм по чистовым поверхностям; отметки — в м от ±0,000; высоты Н — от чистого пола помещения до оси изделия, у декора — до центра.
2. Стена Г показана двумя видами: здесь — архитектурная развёртка (мебель, отделка, проёмы, высоты), электроточки и выводы ВК с привязками и таблицей — на листе 97 («Привязки»).
3. Схема мебели, приборов и декора не является технической документацией для производства мебели; габариты — по паспортам изделий (* — высота не задана в проекте, показана по типовому изделию).
4. Облицовка — по сетке швов 2 мм, раскладка от оси стены (треугольник у пола), целые ряды от пола; подрезки — по листу раскладки плитки.
5. Гидроизоляция в 2 слоя, заход на стены 200 мм; над ванной — до 2000 и 300 мм за борт — до облицовки, с актом скрытых работ и тестом проливом (узел — на листе узлов).

1000 мм · печать 1:1

Изм.	Кол.уч	Лист	№ док.	Подп.	Дата
Разраб.		Кырлан А.С.			04.11.26
Пров.					
ГИП					
Н. контр.					
Утв.					

ГД-2026-009-АИ

Квартира 103 м²

Общая площадь 100,72* м² · * размеры со скана, не замерены (реестр — л. 6, 7, К-1)

Дизайн-проект интерьера

Стадия	Лист	Листов
РП	96	120

Развёртка стены Г. Ванная (пом. 6)

М 1:20

Кырлан Александр Сергеевич

выпуск 04.11.2026 № 20cec94f32 · стр. 105 из 130

Привязки электроточек и выводов ВК, стена Г. Ванная (пом. 6)

Ванная (пом. 6) · вид изнутри помещения · привязки в мм, отметки в м · к развёртке на листе 96

ПРЕДВАРИТЕЛЬНО · не для производства работ · открыто пунктов: 8 (реестр — л. 6, 7)

Развёртка стены Г: электроточки и выводы

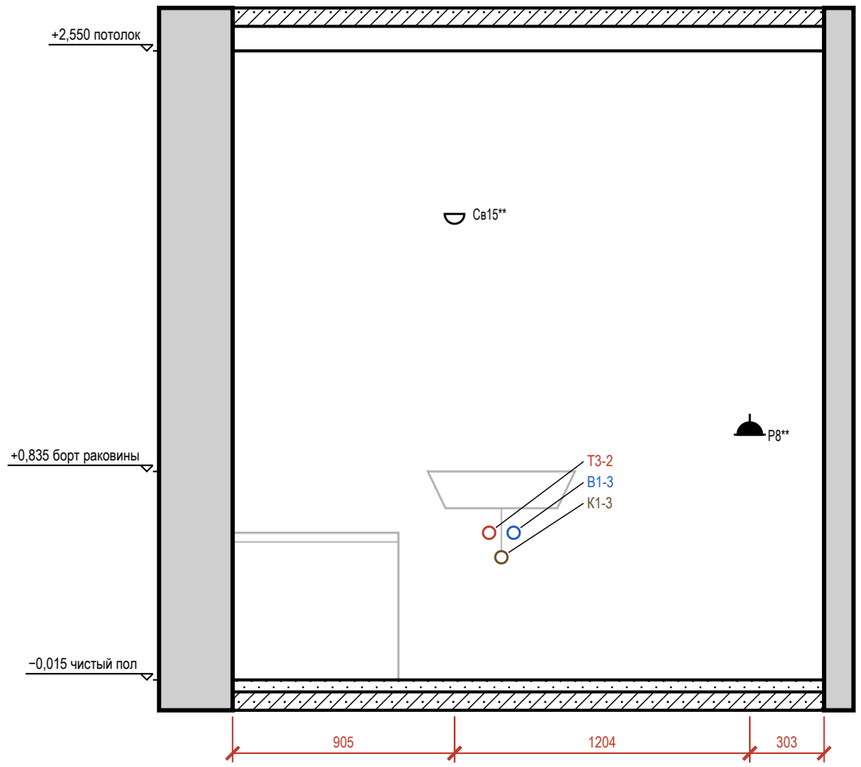



Таблица привязок электроточек и выводов

Марка	Назначение	От угла, мм	Н от пола, мм	Примечание
Св15**	светильник настенный	905	1900	гр. 3
Т3-2	горячая вода — умывальник	1046	600*	межос. 100
К1-3	канализация — умывальник	1096	500*	Ø50
В1-3	холодная вода — умывальник	1146	600*	межос. 100
Р8**	розетка: фен у умывальника	2109	1000	гр. 7, IP44

Условные обозначения

- розетка влагозащищённая IP44
- светильник настенный (бра), Н — высота оси
- вывод В1 (код — в ведомости привязок)
- вывод Т3 (код — в ведомости привязок)
- вывод К1 (код — в ведомости привязок)
- привязки точек и выводов от угла и от пола, мм
- марка развёртки: буква стены, стрелка — взгляд

Схема развёрток (М 1:50)

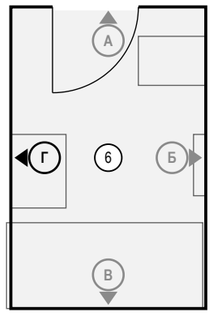

Примечания

1. Вид «Привязки» стены Г — электроточки и выводы ВК; архитектурная развёртка (мебель, отделка, проёмы, высоты) — на листе 96, расположение — на листе 79. Мебель и приборы — подложкой для ориентира; их марки и обозначения мебели, проёмов и стен — там же.
2. Привязки — в мм: по горизонтали от левого чистового угла стены до оси изделия, Н — от чистого пола до оси; все точки — в таблице привязок. Красная цепочка — привязки по осям; точки ближе 150 мм одна к другой в цепочку не дробятся — их привязки только в таблице.
3. У знака — марка электроточки (Р — розетка, S — выключатель, Св — светильник, ЭВ — вывод кабеля); посты в рамке и группа щита — в графе «Примечание»; группы по клавишам выключателя — на листе выключателей.
4. Коды выводов ВК: В1 — холодная вода, Т3 — горячая вода, К1 — канализация; номер после дефиса — номер вывода на листе выводов сантехники; * — высота принята по типовой практике монтажа, окончательно — по паспорту прибора.

Допущения и предложения на листе

Основа листа: размеры сняты со скана обмерного плана KV design (см): часть подписей не читается, помещения выровнены по читаемым размерам; контрольный обмер не выполнен (К-1); высота потолка 2650 мм принята по отметкам обмера (Н = 2,50…2,66 м, ригель 2,28 м) — уточнить при обмере (К-2); толщины стен 300 / 120 мм приняты, межквартирная стена и колонны — по скану, не замерены (К-1); разрешённая мощность 15 кВт принята по типовым ТУ; при объединении двух квартир — переоформление ТУ (К-4); подрайон климата не задан — принят не северный (жилые от 2,5 м) (К-8).

Знак «**» — предложение проектировщика, заказчиком не утверждено (согласовать с заказчиком): Св15 — Сдвиг под раскладку плитки стены Г на 141 мм вдоль стены — ось на шве или в центре плитки, привязка по таблице листа; ИЗ-1: Р8 — по образцу: Р7, Р8 и Р33 на высоте 1000 мм — верхний предел нормы (ПУЭ, п. 6.6.30, не выше 1 м); флаг решения снят; сдвиг под раскладку плитки стены Г на 87 мм вдоль стены — ось на шве или в центре плитки, привязка по таблице листа.

См. лист открытых вопросов (лист 6, записи ИЗ-1, К-1, К-2, К-4, К-8).

1000 мм · печать 1:1

Изм.	Кол.уч	Лист	№ док.	Подп.	Дата
Разраб.		Кырлан А.С.			04.11.26
Пров.					
ГИП					
Н. контр.					
Утв.					

ГД-2026-009-АИ

Квартира 103 м²

Общая площадь 100,72* м² · * размеры со скана, не замерены (реестр — л. 6, 7, К-1)

Дизайн-проект интерьера

Стадия	Лист	Листов
РП	97	120

Привязки электроточек и выводов ВК, стена Г.
Ванная (пом. 6)
М 1:25

Кырлан Александр Сергеевич


выпуск 04.11.2026 № 20cec94f32 · стр. 106 из 130

Развёртки стен. Постирочная (пом. 7)

Постирочная (пом. 7) · вид изнутри помещения · размеры в мм, отметки в м


ПРЕДВАРИТЕЛЬНО · не для производства работ · открыто пунктов: 8 (реестр — л. 6, 7)

Развёртка стены А

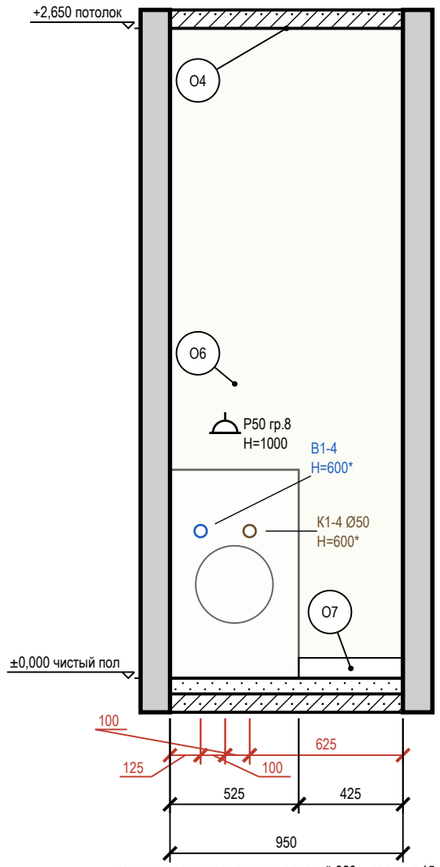


между чистовыми гранями: черновой 980 − отделка 15 / 15

Развёртка стены Б

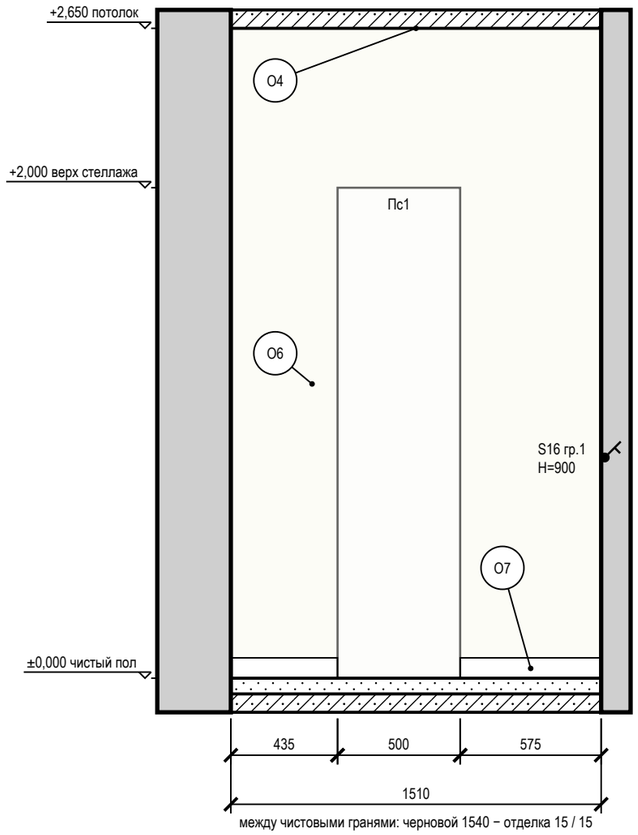


между чистовыми гранями: черновой 1540 − отделка 15 / 15

Развёртка стены В

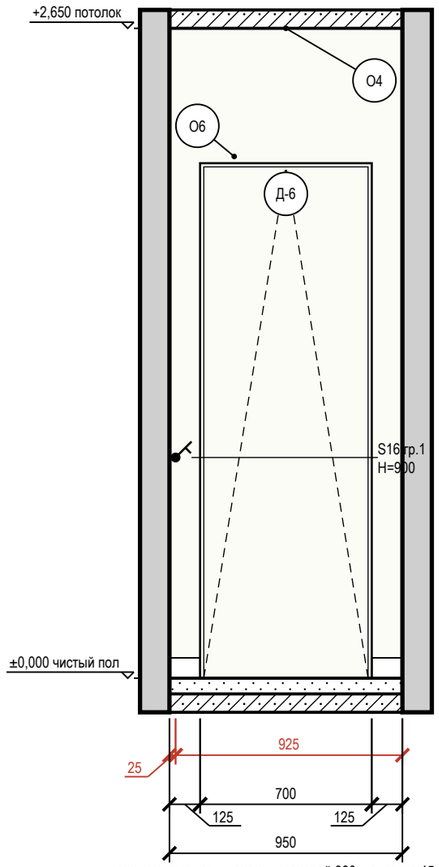


между чистовыми гранями: черновой 980 − отделка 15 / 15

Развёртка стены Г

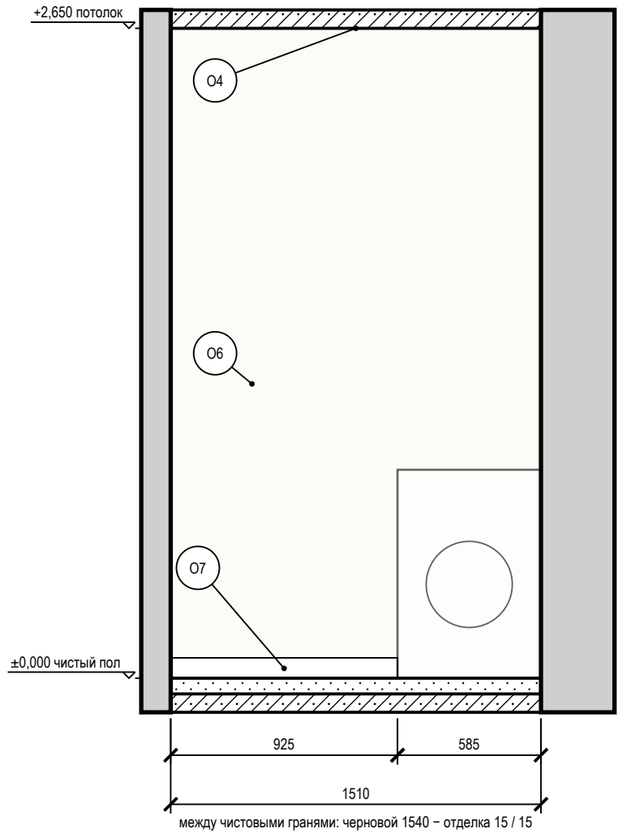

между чистовыми гранями: черновой 1540 − отделка 15 / 15

Схема развёрток (М 1:100)

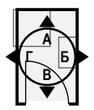

Условные обозначения

- розетка с заземляющим контактом; у знака — марка, ×N постов в рамке, гр. — группа щита, Н — высота оси, мм
- выключатель одноклавишный
- вывод В1 (код — в ведомости привязок)
- вывод К1 (код — в ведомости привязок)
- привязки точек и выводов от угла и от пола, мм
- мебель и приборы — фасад по расстановке (условно)
- дверь скрытого монтажа: полотно в плоскости стены (узел — на листе узлов)
- стены и перекрытия в сечении
- окраска: тон — цвет по коду производителя (условно)
- О1 — марка отделки по реестру отделки альбома
- А — марка развёртки: буква стены, стрелка — взгляд

Допущения и предложения на листе

Основа листа: размеры сняты со скана обмерного плана KV design (см): часть подписей не читается, помещения выровнены по читаемым размерам; контрольный обмер не выполнен (К-1); высота потолка 2650 мм принята по отметкам обмера (Н = 2,50…2,66 м, ригель 2,28 м) — уточнить при обмере (К-2); толщины стен 300 / 120 мм приняты, межквартирная стена и колонны — по скану, не замерены (К-1); разрешённая мощность 15 кВт принята по типовым ТУ; при объединении двух квартир — переоформление ТУ (К-4); подрайон климата не задан — принят не северный (жилые от 2,5 м) (К-8).

См. лист открытых вопросов (лист 6, записи К-1, К-2, К-4, К-8).

Примечания

1. Развёртки — вид на стену изнутри помещения, по часовой стрелке; расположение — на схеме листа и на листе 79; размеры — в мм по чистовым поверхностям; отметки — в м от ±0,000; высоты Н — от чистого пола помещения до оси изделия, у декора — до центра.
2. Красная цепочка — привязки электроточек и выводов по осям от угла чистовых стен; высота Н — у знака, от чистого пола до оси; высоты мебели, проёмов и границ отделки — колонкой отметок слева. Стена с 5 и более точками или с мелкими звеньями привязок показана двумя видами: архитектурная развёртка (мебель, отделка, проёмы, высоты) и вид «Привязки» на отдельном листе — точки и выводы с марками, одна цепочка по осям и таблица привязок (каждая точка — строка).
3. У знака электроточки: марка (Р — розетка, S — выключатель, Св — светильник, ЭВ — вывод кабеля), ×N — число постов в рамке, гр. — группа щита, Н — высота оси от чистого пола, мм; группы по клавишам выключателя — на листе выключателей.
4. Схема мебели, приборов и декора не является технической документацией для производства мебели; габариты — по паспортам изделий (* — высота не задана в проекте, показана по типовому изделию).
5. Выводы ВК — коды и высоты по листу выводов сантехники; * — высота принята по типовой практике монтажа, окончательно — по паспорту прибора.
6. Двери скрытого монтажа — полотно в плоскости стены, отделка стены по полотну, плинтус прерывается у короба (узел — на листе узлов).

1000 мм · печать 1:1

Изм.	Кол.уч	Лист	№ док.	Подп.	Дата
Разраб.		Кырлан А.С.			04.11.26
Пров.					
ГИП					
Н. контр.					
Утв.					

ГД-2026-009-АИ

Квартира 103 м²

Общая площадь 100,72* м² · * размеры со скана, не замерены (реестр — л. 6, 7, К-1)

Дизайн-проект интерьера

Стадия	Лист	Листов
РП	98	120

Развёртки стен. Постирочная (пом. 7)

М 1:25

Кырлан Александр Сергеевич


выпуск 04.11.2026 № 20cec94f32 · стр. 107 из 130

Развёртки стен А, Б. Спальня 2 (пом. 8)

Спальня 2 (пом. 8) · вид изнутри помещения · размеры в мм, отметки в м


ПРЕДВАРИТЕЛЬНО · не для производства работ · открыто пунктов: 8 (реестр — л. 6, 7)

Развёртка стены А

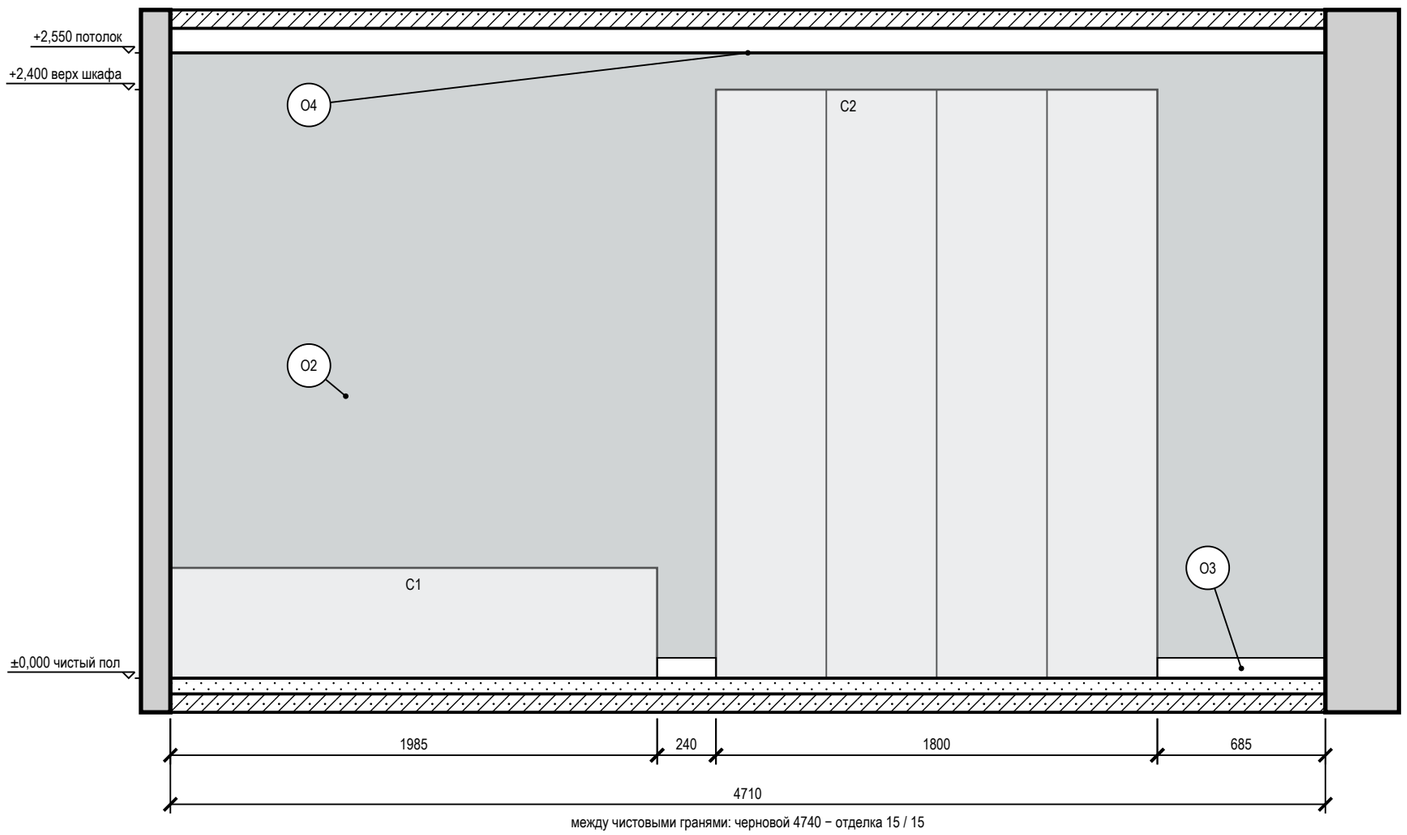


между чистовыми гранями: черновой 4740 − отделка 15 / 15

Развёртка стены Б

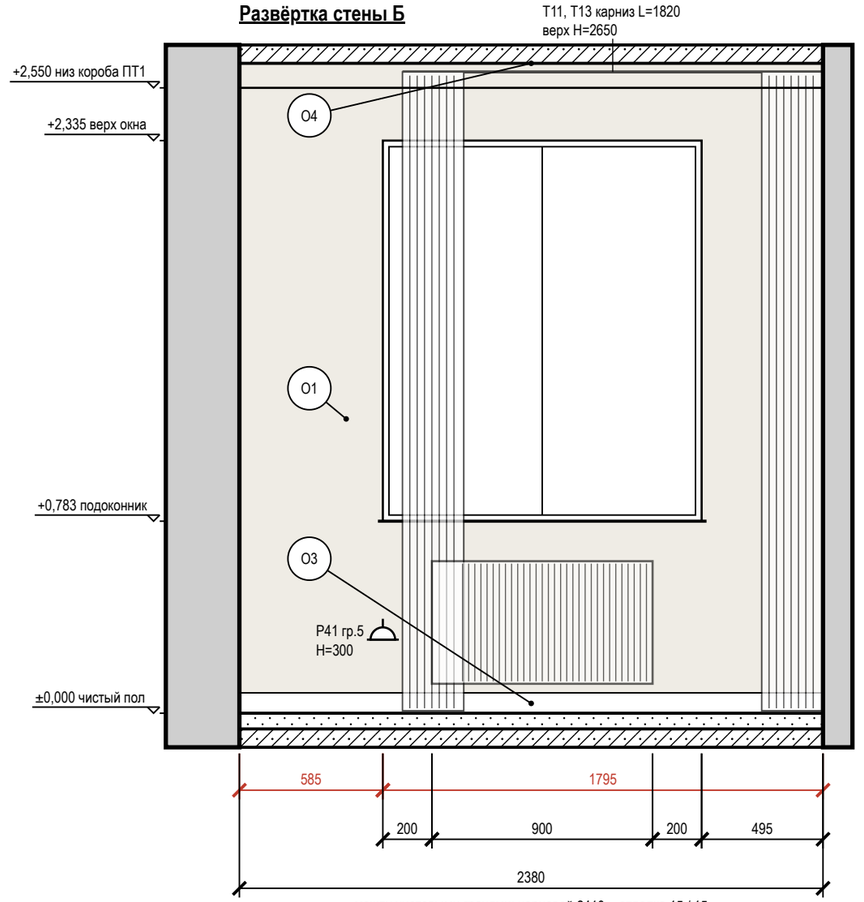

между чистовыми гранями: черновой 2410 − отделка 15 / 15

Схема развёрток (М 1:100)

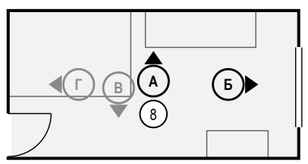

Условные обозначения

- розетка с заземляющим контактом; у знака — марка, ×N постов в рамке, гр. — группа щита, Н — высота оси, мм
- привязки точек и выводов от угла и от пола, мм
- мебель и приборы — фасад по расстановке (условно)
- карниз (шина) и шторы в собранном виде: марка Т, длина L, верх Н
- окно: проём, рама, подоконник
- радиатор отопления; марка — по плану отопления
- стены и перекрытия в сечении
- окраска: тон — цвет по коду производителя (условно)
- О1 — марка отделки по реестру отделки альбома
- А — марка развёртки: буква стены, стрелка — взгляд

Допущения и предложения на листе

Основа листа: размеры сняты со скана обмерного плана KV design (см): часть подписей не читается, помещения выровнены по читаемым размерам; контрольный обмер не выполнен (К-1); высота потолка 2650 мм принята по отметкам обмера (Н = 2,50…2,66 м, ригель 2,28 м) — уточнить при обмере (К-2); толщины стен 300 / 120 мм приняты, межквартирная стена и колонны — по скану, не замерены (К-1); разрешённая мощность 15 кВт принята по типовым ТУ; при объединении двух квартир — переоформление ТУ (К-4); подрайон климата не задан — принят не северный (жилые от 2,5 м) (К-8).

См. лист открытых вопросов (лист 6, записи К-1, К-2, К-4, К-8).

Примечания

1. Развёртки — вид на стену изнутри помещения, по часовой стрелке; расположение — на схеме листа и на листе 79; размеры — в мм по чистовым поверхностям; отметки — в м от ±0,000; высоты Н — от чистого пола помещения до оси изделия, у декора — до центра.
2. Красная цепочка — привязки электроточек и выводов по осям от угла чистовых стен; высота Н — у знака, от чистого пола до оси; высоты мебели, проёмов и границ отделки — колонкой отметок слева. Стена с 5 и более точками или с мелкими звеньями привязок показана двумя видами: архитектурная развёртка (мебель, отделка, проёмы, высоты) и вид «Привязки» на отдельном листе — точки и выводы с марками, одна цепочка по осям и таблица привязок (каждая точка — строка).
3. У знака электроточки: марка (Р — розетка, S — выключатель, Св — светильник, ЭВ — вывод кабеля), ×N — число постов в рамке, гр. — группа щита, Н — высота оси от чистого пола, мм; группы по клавишам выключателя — на листе выключателей.
4. Схема мебели, приборов и декора не является технической документацией для производства мебели; габариты — по паспортам изделий.
5. Карнизы (шины) — по ведомости текстиля декоратора: длина L и верх Н на развёртке — те же числа, что в ведомости; крепление — до окраски потолка.
6. Карниз Т11, Т13: по ведомости текстиля шина L=1820 мм, а от её начала до чистового угла стены — 1715 мм: шина не встаёт, длину согласовать с декоратором до заказа.
7. Линии узора (швы плитки, складки штор, рёбра радиаторов) прерываются у знаков и выносок — просвет между линиями не менее 0,7 мм.

1000 мм · печать 1:1

Изм.	Кол.уч	Лист	№ док.	Подп.	Дата
Разраб.		Кырлан А.С.			04.11.26
Пров.					
ГИП					
Н. контр.					
Утв.					

ГД-2026-009-АИ

Квартира 103 м²

Общая площадь 100,72* м² · * размеры со скана, не замерены (реестр — л. 6, 7, К-1)

Дизайн-проект интерьера

Стадия	Лист	Листов
РП	99	120

Развёртки стен А, Б. Спальня 2 (пом. 8)

М 1:25

Кырлан Александр Сергеевич


выпуск 04.11.2026 № 20cec94f32 · стр. 108 из 130

Развёртка стены В. Спальня 2 (пом. 8)

Спальня 2 (пом. 8) · вид изнутри помещения · размеры в мм, отметки в м


ПРЕДВАРИТЕЛЬНО · не для производства работ · открыто пунктов: 8 (реестр — л. 6, 7)

Развёртка стены В

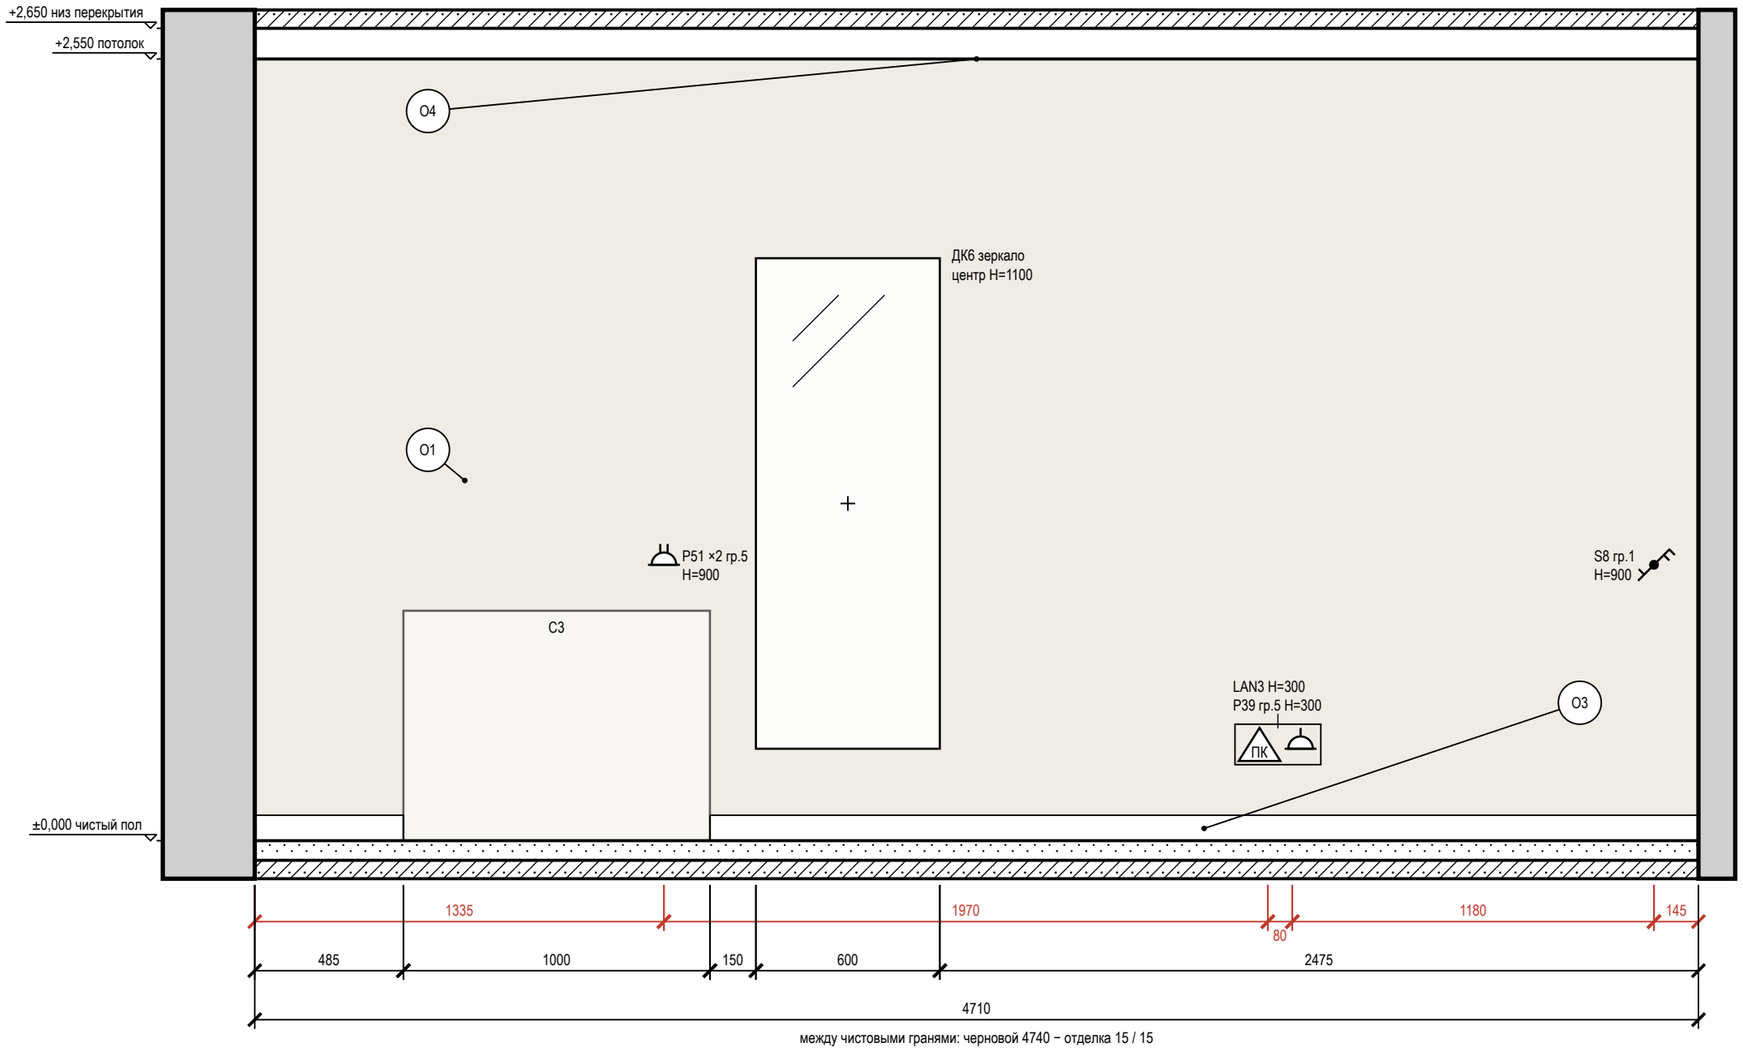

между чистовыми гранями: черновой 4740 − отделка 15 / 15

Схема развёрток (М 1:100)

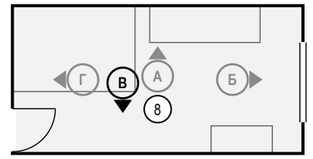

Условные обозначения

- розетка с заземляющим контактом; у знака — марка, ×N постов в рамке, гр. — группа щита, Н — высота оси, мм
- выключатель одноклавишный
- выключатель двухклавишный (флажков — по числу клавиш)
- выключатель с проходной или перекрёстной клавишей (обратный флажок); тип клавиши — в подписи
- ПК — розетка компьютерная RJ45
- привязки точек и выводов от угла и от пола, мм
- мебель и приборы — фасад по расстановке (условно)
- зеркало: марка Д, крест — центр, Н — высота центра, мм
- стены и перекрытия в сечении
- окраска: тон — цвет по коду производителя (условно)
- О1 — марка отделки по реестру отделки альбома
- А — марка развёртки: буква стены, стрелка — взгляд

Допущения и предложения на листе

Основа листа: размеры сняты со скана обмерного плана KV design (см): часть подписей не читается, помещения выровнены по читаемым размерам; контрольный обмер не выполнен (К-1); высота потолка 2650 мм принята по отметкам обмера (Н = 2,50…2,66 м, ригель 2,28 м) — уточнить при обмере (К-2); толщины стен 300 / 120 мм приняты, межквартирная стена и колонны — по скану, не замерены (К-1); разрешённая мощность 15 кВт принята по типовым ТУ; при объединении двух квартир — переоформление ТУ (К-4); подрайон климата не задан — принят не северный (жилые от 2,5 м) (К-8).

См. лист открытых вопросов (лист 6, записи К-1, К-2, К-4, К-8).

Примечания

1. Развёртки — вид на стену изнутри помещения, по часовой стрелке; расположение — на схеме листа и на листе 79; размеры — в мм по чистовым поверхностям; отметки — в м от ±0,000; высоты Н — от чистого пола помещения до оси изделия, у декора — до центра.
2. Красная цепочка — привязки электроточек и выводов по осям от угла чистовых стен; высота Н — у знака, от чистого пола до оси; высоты мебели, проёмов и границ отделки — колонкой отметок слева. Стена с 5 и более точками или с мелкими звеньями привязок показана двумя видами: архитектурная развёртка (мебель, отделка, проёмы, высоты) и вид «Привязки» на отдельном листе — точки и выводы с марками, одна цепочка по осям и таблица привязок (каждая точка — строка).
3. У знака электроточки: марка (Р — розетка, S — выключатель, Св — светильник, ЭВ — вывод кабеля), ×N — число постов в рамке, гр. — группа щита, Н — высота оси от чистого пола, мм; группы по клавишам выключателя — на листе выключателей.
4. Схема мебели, приборов и декора не является технической документацией для производства мебели; габариты — по паспортам изделий.
5. Картины и зеркала крепить к основанию по паспорту изделия (закладные и анкеры — в перечне скрытых работ); крест — ось центра предмета.

1000 мм · печать 1:1

Изм.	Кол.уч	Лист	№ док.	Подп.	Дата
Разраб.		Кырлан А.С.			04.11.26
Пров.					
ГИП					
Н. контр.					
Утв.					

ГД-2026-009-АИ

Квартира 103 м²

Общая площадь 100,72* м² · * размеры со скана, не замерены (реестр — л. 6, 7, К-1)

Дизайн-проект интерьера

Стадия	Лист	Листов
РП	100	120

Развёртка стены В. Спальня 2 (пом. 8)

М 1:20


Кырлан Александр Сергеевич

выпуск 04.11.2026 № 20cec94f32 · стр. 109 из 130

Развёртка стены Г. Спальня 2 (пом. 8)


Спальня 2 (пом. 8) · вид изнутри помещения · размеры в мм, отметки в м

Развёртка стены Г

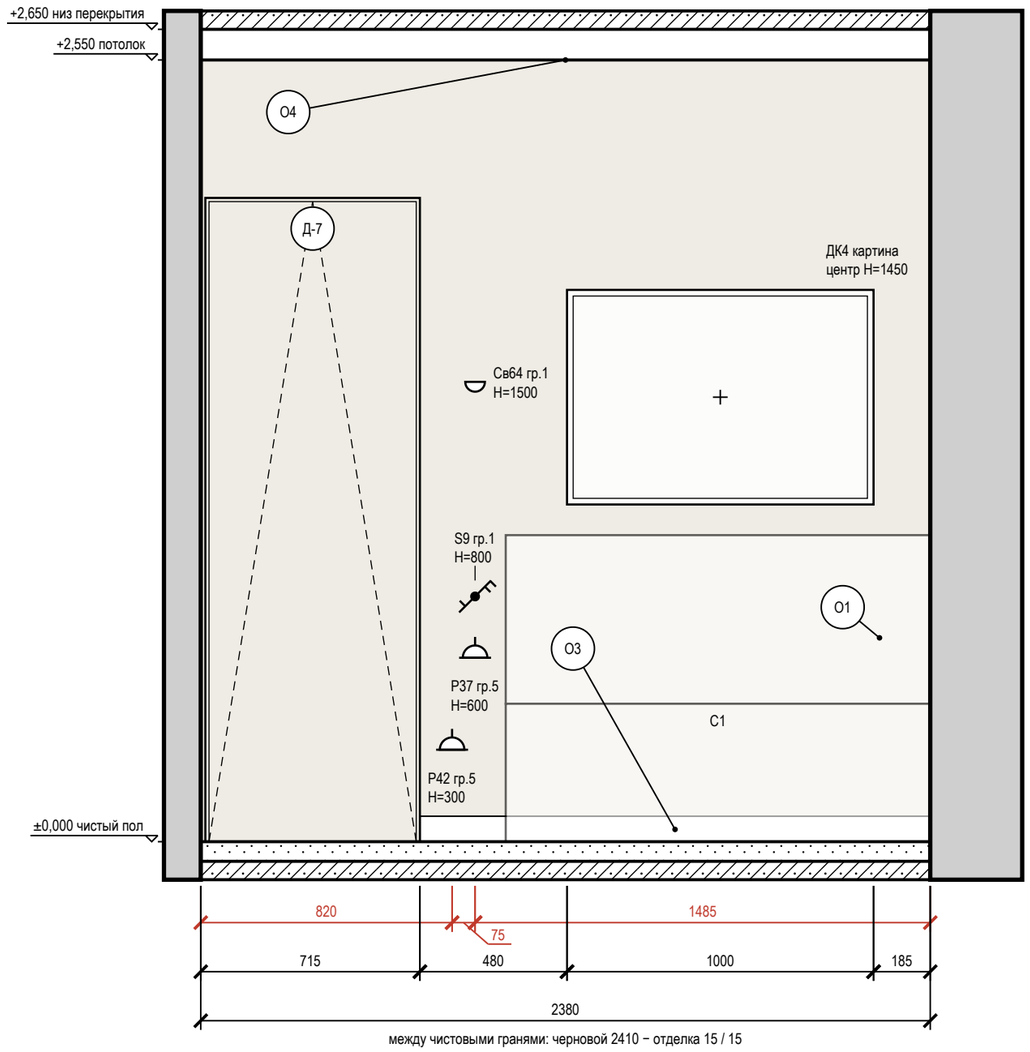

между чистовыми гранями: черновой 2410 − отделка 15 / 15

Схема развёрток (М 1:100)

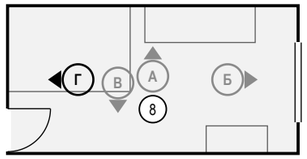

Условные обозначения

- розетка с заземляющим контактом; у знака — марка, ×N постов в рамке, гр. — группа щита, Н — высота оси, мм
- выключатель одноклавишный
- выключатель двухклавишный (флажков — по числу клавиш)
- выключатель с проходной или перекрёстной клавишей (обратный флажок); тип клавиши — в подписи
- светильник настенный (бра), Н — высота оси
- привязки точек и выводов от угла и от пола, мм
- мебель и приборы — фасад по расстановке (условно)
- картина (декор): марка Д, крест — центр, Н — высота центра, мм
- дверь скрытого монтажа: полотно в плоскости стены (узел — на листе узлов)
- стены и перекрытия в сечении
- окраска: тон — цвет по коду производителя (условно)
- О1 — марка отделки по реестру отделки альбома
- А — марка развёртки: буква стены, стрелка — взгляд

Ведомость отделки (на листе)

Марка	Поверхность	Материал, изделие	Цвет, код	Кол.
О1	стены	окраска, Farrow & Ball Modern Emulsion, матовая, подготовка Q3	Farrow & Ball No. 291 «School House White тёплый меловой белый»	4,6 м²
О3	плинтус	плинтус МДФ, h 83 мм, Ultrawood Base 5340, ЛДФ под окраску, 83×15 мм, 2440 мм (арт. LDF-BASE-5340)	Farrow & Ball No. 291 «School House White тёплый меловой белый»	1,7 м
О4	потолок	окраска, Tikkurila Anti-Reflex 2, глубокоматовая, подготовка Q3	NCS S 0502-Y «Белый с лёгкой желтизной»	11,4 м²

Допущения и предложения на листе

Основа листа: размеры сняты со скана обмерного плана KV design (см): часть подписей не читается, помещения выровнены по читаемым размерам; контрольный обмер не выполнен (К-1); высота потолка 2650 мм принята по отметкам обмера (Н = 2,50…2,66 м, ригель 2,28 м) — уточнить при обмере (К-2); толщины стен 300 / 120 мм приняты, межквартирная стена и колонны — по скану, не замерены (К-1); разрешённая мощность 15 кВт принята по типовым ТУ; при объединении двух квартир — переоформление ТУ (К-4); подрайон климата не задан — принят не северный (жилые от 2,5 м) (К-8).

См. лист открытых вопросов (лист 6, записи К-1, К-2, К-4, К-8).

Примечания

1. Развёртки — вид на стену изнутри помещения, по часовой стрелке; расположение — на схеме листа и на листе 79; размеры — в мм по чистовым поверхностям; отметки — в м от ±0,000; высоты Н — от чистого пола помещения до оси изделия, у декора — до центра.
2. Красная цепочка — привязки электроточек и выводов по осям от угла чистовых стен; высота Н — у знака, от чистого пола до оси; высоты мебели, проёмов и границ отделки — колонкой отметок слева. Стена с 5 и более точками или с мелкими звеньями привязок показана двумя видами: архитектурная развёртка (мебель, отделка, проёмы, высоты) и вид «Привязки» на отдельном листе — точки и выводы с марками, одна цепочка по осям и таблица привязок (каждая точка — строка).
3. У знака электроточки: марка (Р — розетка, S — выключатель, Св — светильник, ЭВ — вывод кабеля), ×N — число постов в рамке, гр. — группа щита, Н — высота оси от чистого пола, мм; группы по клавишам выключателя — на листе выключателей.
4. Схема мебели, приборов и декора не является технической документацией для производства мебели; габариты — по паспортам изделий.
5. Картины и зеркала крепить к основанию по паспорту изделия (закладные и анкеры — в перечне скрытых работ); крест — ось центра предмета.
6. Двери скрытого монтажа — полотно в плоскости стены, отделка стены по полотну, плинтус прерывается у короба (узел — на листе узлов).

1000 мм · печать 1:1

Изм.	Кол.уч	Лист	№ док.	Подп.	Дата
Разраб.		Кырлан А.С.			04.11.26
Пров.					
ГИП					
Н. контр.					
Утв.					

ГД-2026-009-АИ

Квартира 103 м²

Общая площадь 100,72* м² · * размеры со скана, не замерены (реестр — л. 6, 7, К-1)

Дизайн-проект интерьера

Стадия	Лист	Листов
РП	101	120

Развёртка стены Г. Спальня 2 (пом. 8)

М 1:20


Кырлан Александр Сергеевич

выпуск 04.11.2026 № 20cec94f32 · стр. 110 из 130

Развёртка стены А. Коридор (пом. 9)

Коридор (пом. 9) · вид изнутри помещения · размеры в мм, отметки в м

Развёртка стены А

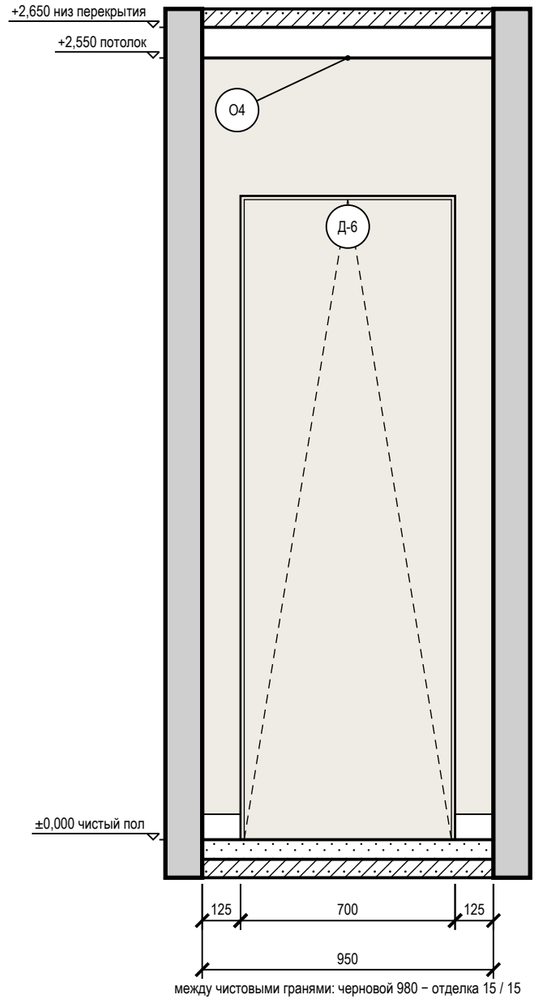

между чистовыми гранями: черновой 980 − отделка 15 / 15

Схема развёрток (М 1:100)



Условные обозначения

- мебель и приборы — фасад по расстановке (условно)
- дверь скрытого монтажа: полотно в плоскости стены (узел — на листе узлов)
- стены и перекрытия в сечении
- окраска: тон — цвет по коду производителя (условно)
- О1 — марка отделки по реестру отделки альбома
- А — марка развёртки: буква стены, стрелка — взгляд

Ведомость отделки (на листе)

Марка	Поверхность	Материал, изделие	Цвет, код	Кол.
О1	стены	окраска, Farrow & Ball Modern Emulsion, матовая, подготовка Q3	Farrow & Ball No. 291 «School House White — тёплый меловой белый»	1 м²
О3	плинтус	плинтус МДФ, h 83 мм, Ultrawood Base 5340, ЛДФ под окраску, 83×15 мм, 2440 мм (арт. LDF-BASE-5340)	Farrow & Ball No. 291 «School House White — тёплый меловой белый»	0,3 м
О4	потолок	окраска, Tikkurila Anti-Reflex 2, глубокоматовая, подготовка Q3	NCS S 0502-Y «Белый с лёгкой желтизной»	6 м²

Примечания

1. Развёртки — вид на стену изнутри помещения, по часовой стрелке; расположение — на схеме листа и на листе 79; размеры — в мм по чистовым поверхностям; отметки — в м от ±0,000; высоты Н — от чистого пола помещения до оси изделия, у декора — до центра.
2. Схема мебели, приборов и декора не является технической документацией для производства мебели; габариты — по паспортам изделий.
3. Двери скрытого монтажа — полотно в плоскости стены, отделка стены по полотну, плинтус прерывается у короба (узел — на листе узлов).

Допущения и предложения на листе

Основа листа: размеры сняты со скана обмерного плана KV design (см): часть подписей не читается, помещения выровнены по читаемым размерам; контрольный обмер не выполнен (К-1); высота потолка 2650 мм принята по отметкам обмера (Н = 2,50…2,66 м, ригель 2,28 м) — уточнить при обмере (К-2); толщины стен 300 / 120 мм приняты, межквартирная стена и колонны — по скану, не замерены (К-1); разрешённая мощность 15 кВт принята по типовым ТУ; при объединении двух квартир — переоформление ТУ (К-4); подрайон климата не задан — принят не северный (жилые от 2,5 м) (К-8).
См. лист открытых вопросов (лист 6, записи К-1, К-2, К-4, К-8).

1000 мм · печать 1:1

Изм.	Кол.уч	Лист	№ док.	Подп.	Дата
Разраб.		Кырлан А.С.			04.11.26
Пров.					
ГИП					
Н. контр.					
Утв.					

ГД-2026-009-АИ

Квартира 103 м²

Общая площадь 100,72* м² · * размеры со скана, не замерены (реестр — л. 6, 7, К-1)

Дизайн-проект интерьера	Стадия	Лист	Листов
	РП	102	120
Развёртка стены А. Коридор (пом. 9) М 1:20	**Кырлан Александр Сергеевич**		


выпуск 04.11.2026 № 20cec94f32 · стр. 111 из 130

Развёртка стены Б. Коридор (пом. 9)

Коридор (пом. 9) · вид изнутри помещения · размеры в мм, отметки в м


ПРЕДВАРИТЕЛЬНО · не для производства работ · открыто пунктов: 8 (реестр — л. 6, 7)

Развёртка стены Б

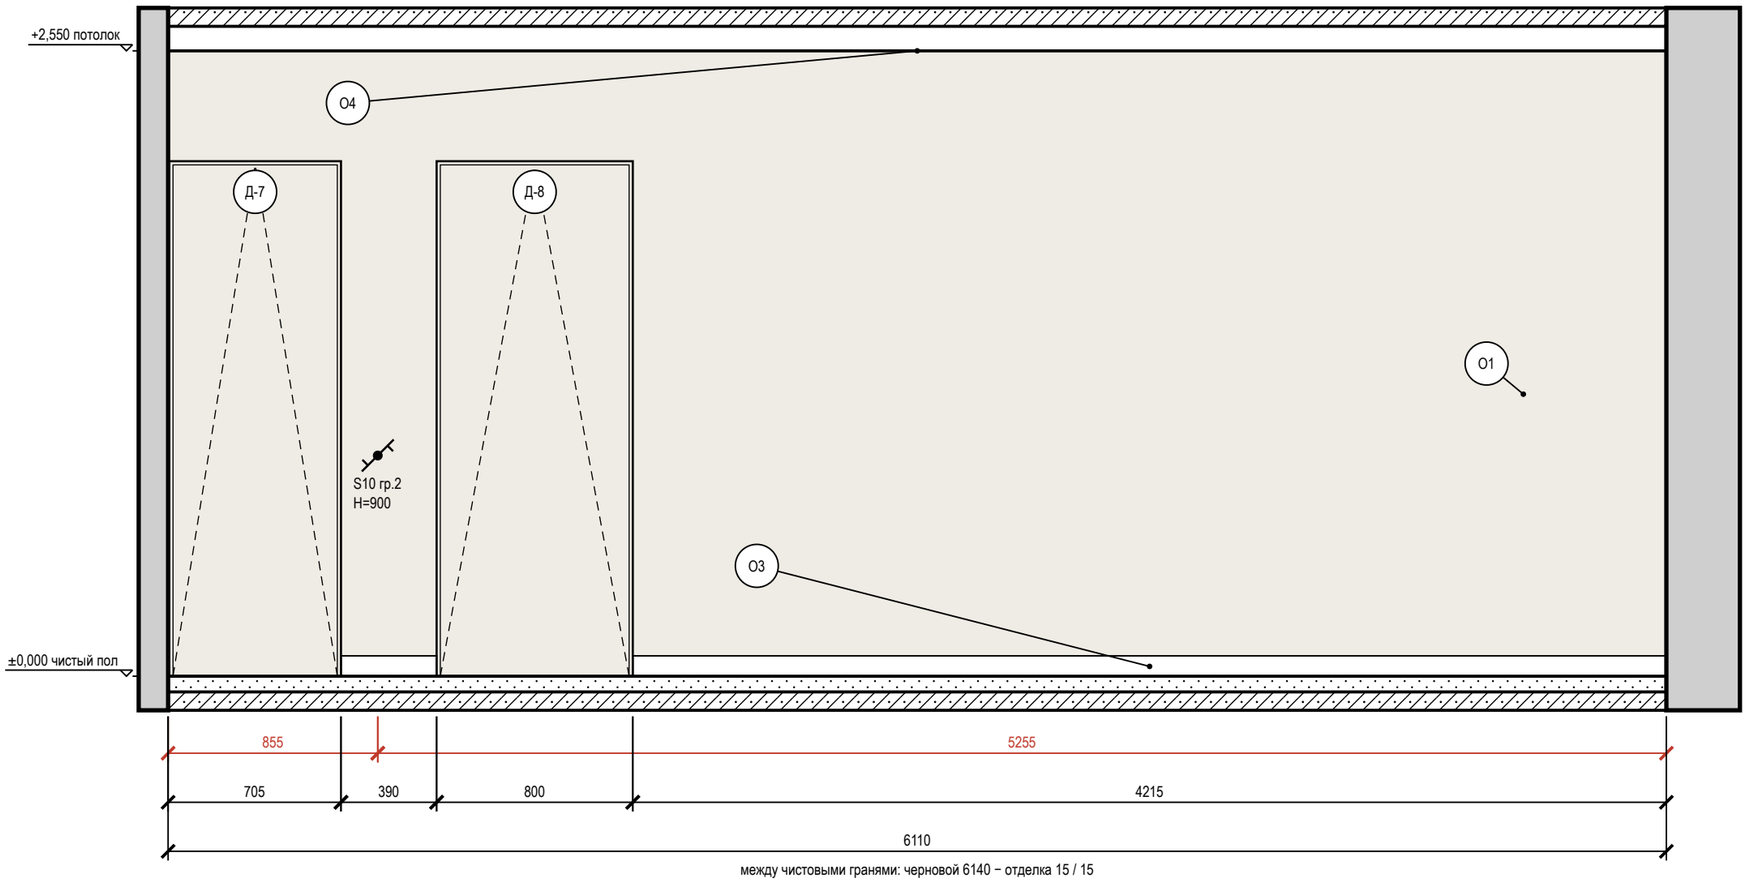

между чистовыми гранями: черновой 6140 − отделка 15 / 15

Схема развёрток (М 1:100)

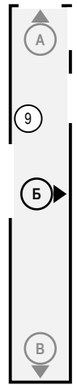

Условные обозначения

- выключатель одноклавишный
- выключатель с проходной или перекрёстной клавишей (обратный флажок); тип клавиши — в подписи
- привязки точек и выводов от угла и от пола, мм
- мебель и приборы — фасад по расстановке (условно)
- дверь скрытого монтажа: полотно в плоскости стены (узел — на листе узлов)
- стены и перекрытия в сечении
- окраска: тон — цвет по коду производителя (условно)
- О1 — марка отделки по реестру отделки альбома
- А — марка развёртки: буква стены, стрелка — взгляд

Ведомость отделки (на листе)

Марка	Поверхность	Материал, изделие	Цвет, код	Кол.
О1	стены	окраска, Farrow & Ball Modern Emulsion, матовая, подготовка Q3	Farrow & Ball No. 291 «School House White тёплый меловой белый»	12,4 м²
О3	плинтус	плинтус МДФ, h 83 мм, Ultrawood Base 5340, ЛДФ под окраску, 83×15 мм, 2440 мм (арт. LDF-BASE-5340)	Farrow & Ball No. 291 «School House White тёплый меловой белый»	4,6 м
О4	потолок	окраска, Tikkurila Anti-Reflex 2, глубокоматовая, подготовка Q3	NCS S 0502-Y «Белый с лёгкой желтизной»	6 м²

Примечания

1. Развёртки — вид на стену изнутри помещения, по часовой стрелке; расположение — на схеме листа и на листе 79; размеры — в мм по чистовым поверхностям; отметки — в м от ±0,000; высоты Н — от чистого пола помещения до оси изделия, у декора — до центра.
2. Красная цепочка — привязки электроточек и выводов по осям от угла чистовых стен; высота Н — у знака, от чистого пола до оси; высоты мебели, проёмов и границ отделки — колонкой отметок слева. Стена с 5 и более точками или с мелкими звеньями привязок показана двумя видами: архитектурная развёртка (мебель, отделка, проёмы, высоты) и вид «Привязки» на отдельном листе — точки и выводы с марками, одна цепочка по осям и таблица привязок (каждая точка — строка).
3. У знака электроточки: марка (Р — розетка, S — выключатель, Св — светильник, ЭВ — вывод кабеля), ×N — число постов в рамке, гр. — группа щита, Н — высота оси от чистого пола, мм; группы по клавишам выключателя — на листе выключателей.
4. Схема мебели, приборов и декора не является технической документацией для производства мебели; габариты — по паспортам изделий.
5. Двери скрытого монтажа — полотно в плоскости стены, отделка стены по полотну, плинтус прерывается у короба (узел — на листе узлов).

1000 мм · печать 1:1

Допущения и предложения на листе

Основа листа: размеры сняты со скана обмерного плана KV design (см): часть подписей не читается, помещения выровнены по читаемым размерам; контрольный обмер не выполнен (К-1); высота потолка 2650 мм принята по отметкам обмера (Н = 2,50…2,66 м, ригель 2,28 м) — уточнить при обмере (К-2); толщины стен 300 / 120 мм приняты, межквартирная стена и колонны — по скану, не замерены (К-1); разрешённая мощность 15 кВт принята по типовым ТУ; при объединении двух квартир — переоформление ТУ (К-4); подрайон климата не задан — принят не северный (жилые от 2,5 м) (К-8).

См. лист открытых вопросов (лист 6, записи К-1, К-2, К-4, К-8).

Изм.	Кол.уч	Лист	№ док.	Подп.	Дата				
Разраб.		Кырлан А.С.			04.11.26	ГД-2026-009-АИ			
Пров.						Квартира 103 м² Общая площадь 100,72* м² · * размеры со скана, не замерены (реестр — л. 6, 7, К-1)			
ГИП						Дизайн-проект интерьера	Стадия: РП	Лист: 103	Листов: 120
Н. контр.						Развёртка стены Б. Коридор (пом. 9) М 1:25	Кырлан Александр Сергеевич		
Утв.									

выпуск 04.11.2026 № 20cec94f32 · стр. 112 из 130

Развёртка стены В. Коридор (пом. 9)

Коридор (пом. 9) · вид изнутри помещения · размеры в мм, отметки в м

ПРЕДВАРИТЕЛЬНО · не для производства работ · открыто пунктов: 8 (реестр — л. 6, 7)

Развёртка стены В

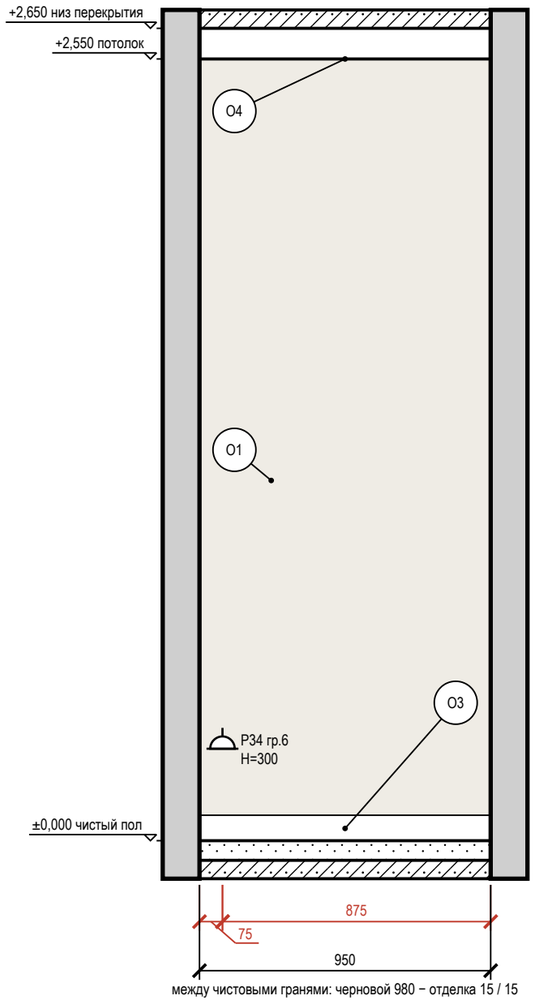


Схема развёрток (М 1:100)



Условные обозначения

- розетка с заземляющим контактом; у знака — марка, ×N постов в рамке, гр. — группа щита, Н — высота оси, мм
- привязки точек и выводов от угла и от пола, мм
- мебель и приборы — фасад по расстановке (условно)
- стены и перекрытия в сечении
- окраска: тон — цвет по коду производителя (условно)
- О1 — марка отделки по реестру отделки альбома
- А — марка развёртки: буква стены, стрелка — взгляд

Ведомость отделки (на листе)

Марка	Поверхность	Материал, изделие	Цвет, код	Кол.
О1	стены	окраска, Farrow & Ball Modern Emulsion, матовая, подготовка Q3	Farrow & Ball No. 291 «School House White тёплый меловой белый»	2,4 м²
О3	плинтус	плинтус МДФ, h 83 мм, Ultrawood Base 5340, ЛДФ под окраску, 83×15 мм, 2440 мм (арт. LDF-BASE-5340)	Farrow & Ball No. 291 «School House White тёплый меловой белый»	0,9 м
О4	потолок	окраска, Tikkurila Anti-Reflex 2, глубокоматовая, подготовка Q3	NCS S 0502-Y «Белый с лёгкой желтизной»	6 м²

Допущения и предложения на листе

Основа листа: размеры сняты со скана обмерного плана KV design (см): часть подписей не читается, помещения выровнены по читаемым размерам; контрольный обмер не выполнен (К-1); высота потолка 2650 мм принята по отметкам обмера (Н = 2,50…2,66 м, ригель 2,28 м) — уточнить при обмере (К-2); толщины стен 300 / 120 мм приняты, межквартирная стена и колонны — по скану, не замерены (К-1); разрешённая мощность 15 кВт принята по типовым ТУ; при объединении двух квартир — переоформление ТУ (К-4); подрайон климата не задан — принят не северный (жилые от 2,5 м) (К-8).

См. лист открытых вопросов (лист 6, записи К-1, К-2, К-4, К-8).

Примечания

1. Развёртки — вид на стену изнутри помещения, по часовой стрелке; расположение — на схеме листа и на листе 79; размеры — в мм по чистовым поверхностям; отметки — в м от ±0,000; высоты Н — от чистого пола помещения до оси изделия, у декора — до центра.
2. Красная цепочка — привязки электроточек и выводов по осям от угла чистовых стен; высота Н — у знака, от чистого пола до оси; высоты мебели, проёмов и границ отделки — колонкой отметок слева. Стена с 5 и более точками или с мелкими звеньями привязок показана двумя видами: архитектурная развёртка (мебель, отделка, проёмы, высоты) и вид «Привязки» на отдельном листе — точки и выводы с марками, одна цепочка по осям и таблица привязок (каждая точка — строка).
3. У знака электроточки: марка (Р — розетка, S — выключатель, Св — светильник, ЭВ — вывод кабеля), ×N — число постов в рамке, гр. — группа щита, Н — высота оси от чистого пола, мм; группы по клавишам выключателя — на листе выключателей.
4. Схема мебели, приборов и декора не является технической документацией для производства мебели; габариты — по паспортам изделий.

1000 мм · печать 1:1

Изм.	Кол.уч	Лист	№ док.	Подп.	Дата
Разраб.		Кырлан А.С.			04.11.26
Пров.					
ГИП					
Н. контр.					
Утв.					

ГД-2026-009-АИ

Квартира 103 м²

Общая площадь 100,72* м² · * размеры со скана, не замерены (реестр — л. 6, 7, К-1)

Дизайн-проект интерьера

Стадия	Лист	Листов
РП	104	120

Развёртка стены В. Коридор (пом. 9)

М 1:20

Кырлан Александр Сергеевич


выпуск 04.11.2026 № 20cec94f32 · стр. 113 из 130

Развёртка стены А. Спальня мастер (пом. 10)

Спальня мастер (пом. 10) · вид изнутри помещения · размеры в мм, отметки в м


ПРЕДВАРИТЕЛЬНО · не для производства работ · открыто пунктов: 8 (реестр — л. 6, 7)

Развёртка стены А

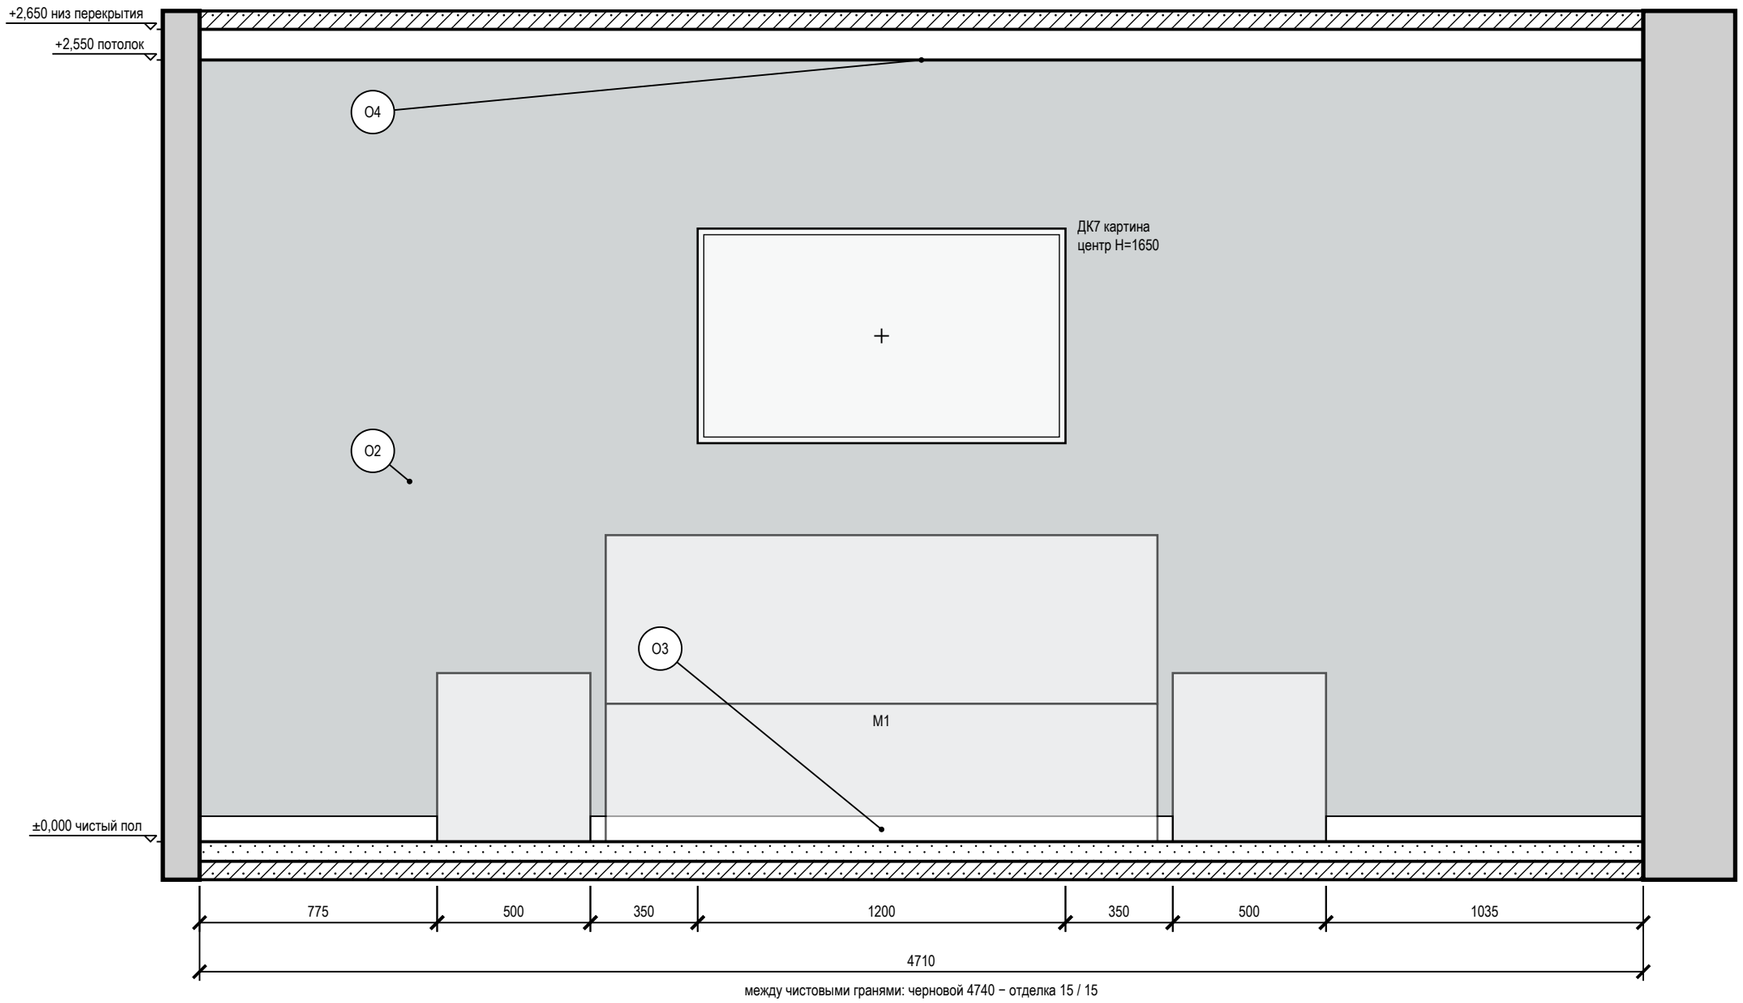

между чистовыми гранями: черновой 4740 − отделка 15 / 15

Схема развёрток (М 1:100)

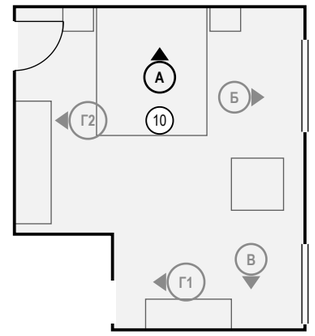

Условные обозначения

- мебель и приборы — фасад по расстановке (условно)
- картина (декор): марка Д, крест — центр, Н — высота центра, мм
- стены и перекрытия в сечении
- окраска: тон — цвет по коду производителя (условно)
- О1 — марка отделки по реестру отделки альбома
- А — марка развёртки: буква стены, стрелка — взгляд

Допущения и предложения на листе

Основа листа: размеры сняты со скана обмерного плана KV design (см): часть подписей не читается, помещения выровнены по читаемым размерам; контрольный обмер не выполнен (К-1); высота потолка 2650 мм принята по отметкам обмера (Н = 2,50…2,66 м, ригель 2,28 м) — уточнить при обмере (К-2); толщины стен 300 / 120 мм приняты, межквартирная стена и колонны — по скану, не замерены (К-1); разрешённая мощность 15 кВт принята по типовым ТУ; при объединении двух квартир — переоформление ТУ (К-4); подрайон климата не задан — принят не северный (жилые от 2,5 м) (К-8).

Знак «*» — принято, не замерено и не подтверждено (замерить на объекте): К-1: окно пом. 10 (стена Б) — Окно 1300 при offset 3500 на стене Б основной части (длина 3830) выходило за стену на 970 мм.

См. лист открытых вопросов (лист 6, записи К-1, К-2, К-4, К-8).

Примечания

1. Развёртки — вид на стену изнутри помещения, по часовой стрелке; расположение — на схеме листа и на листе 79; размеры — в мм по чистовым поверхностям; отметки — в м от ±0,000; высоты Н — от чистого пола помещения до оси изделия, у декора — до центра.
2. Стена А показана двумя видами: здесь — архитектурная развёртка (мебель, отделка, проёмы, высоты), электроточки и выводы ВК с привязками и таблицей — на листе 106 («Привязки»).
3. Схема мебели, приборов и декора не является технической документацией для производства мебели; габариты — по паспортам изделий.
4. Картины и зеркала крепить к основанию по паспорту изделия (закладные и анкеры — в перечне скрытых работ); крест — ось центра предмета.

1000 мм · печать 1:1

Изм.	Кол.уч	Лист	№ док.	Подп.	Дата
Разраб.		Кырлан А.С.			04.11.26
Пров.					
ГИП					
Н. контр.					
Утв.					

ГД-2026-009-АИ

Квартира 103 м²

Общая площадь 100,72* м² · * размеры со скана, не замерены (реестр — л. 6, 7, К-1)

Дизайн-проект интерьера

Стадия	Лист	Листов
РП	105	120

Развёртка стены А. Спальня мастер (пом. 10)

М 1:20

Кырлан Александр Сергеевич

выпуск 04.11.2026 № 20cec94f32 · стр. 114 из 130

Привязки электроточек, стена А. Спальня мастер (пом. 10)

Спальня мастер (пом. 10) · вид изнутри помещения · привязки в мм, отметки в м · к развёртке на листе 105

ПРЕДВАРИТЕЛЬНО · не для производства работ · открыто пунктов: 8 (реестр — л. 6, 7)

Развёртка стены А: электроточки и выводы

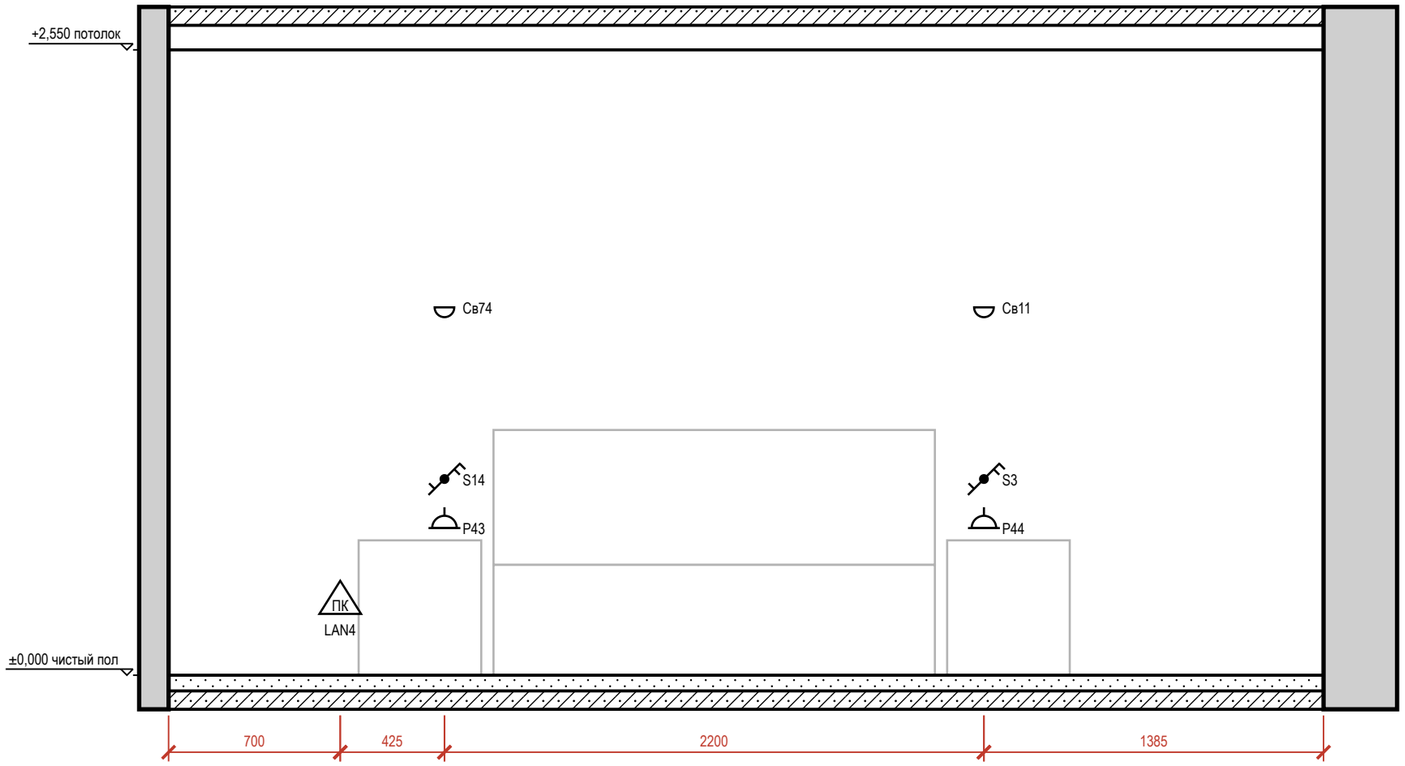



Таблица привязок электроточек и выводов

Марка	Назначение	От угла, мм	Н от пола, мм	Примечание
LAN4	розетка RJ45: передача данных	700	300	
P43	розетка: у кровати	1125	600	гр. 4
S14	выключатель	1125	800	гр. 1
Св74	светильник настенный	1125	1500	гр. 1
P44	розетка: у кровати	3325	600	гр. 4
S3	выключатель	3325	800	гр. 1
Св11	светильник настенный	3325	1500	гр. 1

Условные обозначения

- розетка с заземляющим контактом; у знака — марка, ×N постов в рамке, гр. — группа щита, Н — высота оси, мм
- выключатель одноклавишный
- выключатель двухклавишный (флажков — по числу клавиш)
- выключатель с проходной или перекрёстной клавишей (обратный флажок); тип клавиши — в подписи
- светильник настенный (бра), Н — высота оси
- ПК — розетка компьютерная RJ45
- привязки точек и выводов от угла и от пола, мм
- А — марка развёртки: буква стены, стрелка — взгляд

Схема развёрток (М 1:200)

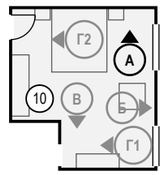

Примечания

1. Вид «Привязки» стены А — электроточки и выводы ВК; архитектурная развёртка (мебель, отделка, проёмы, высоты) — на листе 105, расположение — на листе 79. Мебель и приборы — подложкой для ориентира; их марки и обозначения мебели, проёмов и стен — там же.
2. Привязки — в мм: по горизонтали от левого чистового угла стены до оси изделия, Н — от чистого пола до оси; все точки — в таблице привязок. Красная цепочка — привязки по осям; точки ближе 150 мм одна к другой в цепочку не дробятся — их привязки только в таблице.
3. У знака — марка электроточки (Р — розетка, S — выключатель, Св — светильник, ЭВ — вывод кабеля); посты в рамке и группа щита — в графе «Примечание»; группы по клавишам выключателя — на листе выключателей.

Допущения и предложения на листе

Основа листа: размеры сняты со скана обмерного плана KV design (см): часть подписей не читается, помещения выровнены по читаемым размерам; контрольный обмер не выполнен (К-1); высота потолка 2650 мм принята по отметкам обмера (Н = 2,50…2,66 м, ригель 2,28 м) — уточнить при обмере (К-2); толщины стен 300 / 120 мм приняты, межквартирная стена и колонны — по скану, не замерены (К-1); разрешённая мощность 15 кВт принята по типовым ТУ; при объединении двух квартир — переоформление ТУ (К-4); подрайон климата не задан — принят не северный (жилые от 2,5 м) (К-8).

Знак «*» — принято, не замерено и не подтверждено (замерить на объекте): К-1: окно пом. 10 (стена Б) — Окно 1300 при offset 3500 на стене Б основной части (длина 3830) выходило за стену на 970 мм.

См. лист открытых вопросов (лист 6, записи К-1, К-2, К-4, К-8).

1000 мм · печать 1:1

Изм.	Кол.уч	Лист	№ док.	Подп.	Дата
Разраб.		Кырлан А.С.			04.11.26
Пров.					
ГИП					
Н. контр.					
Утв.					

ГД-2026-009-АИ

Квартира 103 м²

Общая площадь 100,72* м² · * размеры со скана, не замерены (реестр — л. 6, 7, К-1)

Дизайн-проект интерьера

Стадия	Лист	Листов
РП	106	120

Привязки электроточек, стена А. Спальня мастер (пом. 10)

М 1:25

Кырлан Александр Сергеевич


выпуск 04.11.2026 № 20cec94f32 · стр. 115 из 130

Развёртка стены Б. Спальня мастер (пом. 10)

Спальня мастер (пом. 10) · вид изнутри помещения · размеры в мм, отметки в м


ПРЕДВАРИТЕЛЬНО · не для производства работ · открыто пунктов: 8 (реестр — л. 6, 7)

Развёртка стены Б

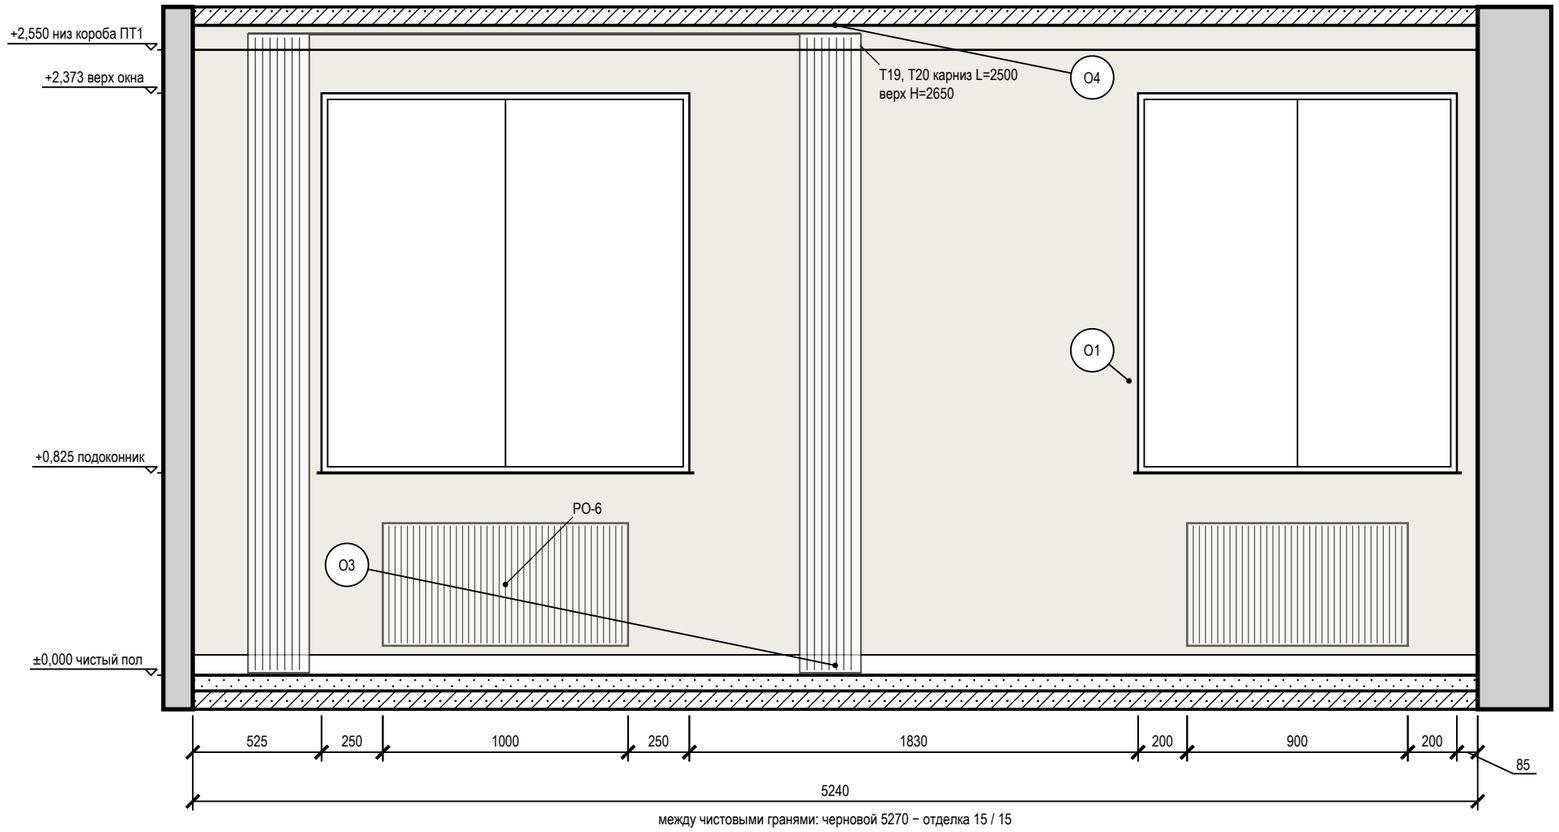

между чистовыми гранями: черновой 5270 − отделка 15 / 15

Схема развёрток (М 1:100)

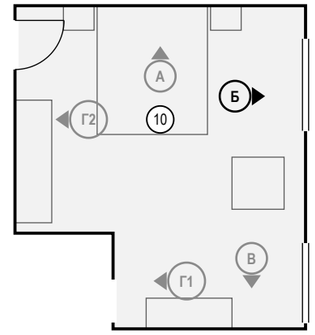

Условные обозначения

- мебель и приборы — фасад по расстановке (условно)
- карниз (шина) и шторы в собранном виде: марка Т, длина L, верх H
- окно: проём, рама, подоконник
- радиатор отопления; марка — по плану отопления
- стены и перекрытия в сечении
- окраска: тон — цвет по коду производителя (условно)
- О1 — марка отделки по реестру отделки альбома
- А — марка развёртки: буква стены, стрелка — взгляд

Ведомость отделки (на листе)

Марка	Поверхность	Материал, изделие	Цвет, код	Кол.
О1	стены	окраска, Farrow & Ball Modern Emulsion, матовая, подготовка Q3	Farrow & Ball No. 291 «School House White — тёплый меловой белый»	9,6 м²
О3	плинтус	плинтус МДФ, h 83 мм, Ultrawood Base 5340, ЛДФ под окраску, 83×15 мм, 2440 мм (арт. LDF-BASE-5340)	Farrow & Ball No. 291 «School House White — тёплый меловой белый»	5,2 м
О4	потолок	окраска, Tikkurila Anti-Reflex 2, глубокоматовая, подготовка Q3	NCS S 0502-Y «Белый с лёгкой желтизной»	22,5 м²

Допущения и предложения на листе

Основа листа: размеры сняты со скана обмерного плана KV design (см): часть подписей не читается, помещения выровнены по читаемым размерам; контрольный обмер не выполнен (К-1); высота потолка 2650 мм принята по отметкам обмера (Н = 2,50…2,66 м, ригель 2,28 м) — уточнить при обмере (К-2); толщины стен 300 / 120 мм приняты, межквартирная стена и колонны — по скану, не замерены (К-1); разрешённая мощность 15 кВт принята по типовым ТУ; при объединении двух квартир — переоформление ТУ (К-4); подрайон климата не задан — принят не северный (жилые от 2,5 м) (К-8).

Знак «*» — принято, не замерено и не подтверждено (замерить на объекте): К-1: окно пом. 10 (стена Б) — Окно 1300 при offset 3500 на стене Б основной части (длина 3830) выходило за стену на 970 мм.

См. лист открытых вопросов (лист 6, записи К-1, К-2, К-4, К-8).

Примечания

1. Развёртки — вид на стену изнутри помещения, по часовой стрелке; расположение — на схеме листа и на листе 79; размеры — в мм по чистовым поверхностям; отметки — в м от ±0,000; высоты Н — от чистого пола помещения до оси изделия, у декора — до центра.
2. Схема мебели, приборов и декора не является технической документацией для производства мебели; габариты — по паспортам изделий.
3. Карнизы (шины) — по ведомости текстиля декоратора: длина L и верх Н на развёртке — те же числа, что в ведомости; крепление — до окраски потолка.

1000 мм · печать 1:1

Изм.	Кол.уч	Лист	№ док.	Подп.	Дата
Разраб.		Кырлан А.С.			04.11.26
Пров.					
ГИП					
Н. контр.					
Утв.					

ГД-2026-009-АИ

Квартира 103 м²

Общая площадь 100,72* м² · * размеры со скана, не замерены (реестр — л. 6, 7, К-1)

Дизайн-проект интерьера

Стадия	Лист	Листов
РП	107	120

Развёртка стены Б. Спальня мастер (пом. 10)

М 1:25

Кырлан Александр Сергеевич


выпуск 04.11.2026 № 20cec94f32 · стр. 116 из 130

Развёртки стен В, Г1. Спальня мастер (пом. 10)

Спальня мастер (пом. 10) · вид изнутри помещения · размеры в мм, отметки в м


ПРЕДВАРИТЕЛЬНО · не для производства работ · открыто пунктов: 8 (реестр — л. 6, 7)

Развёртка стены В

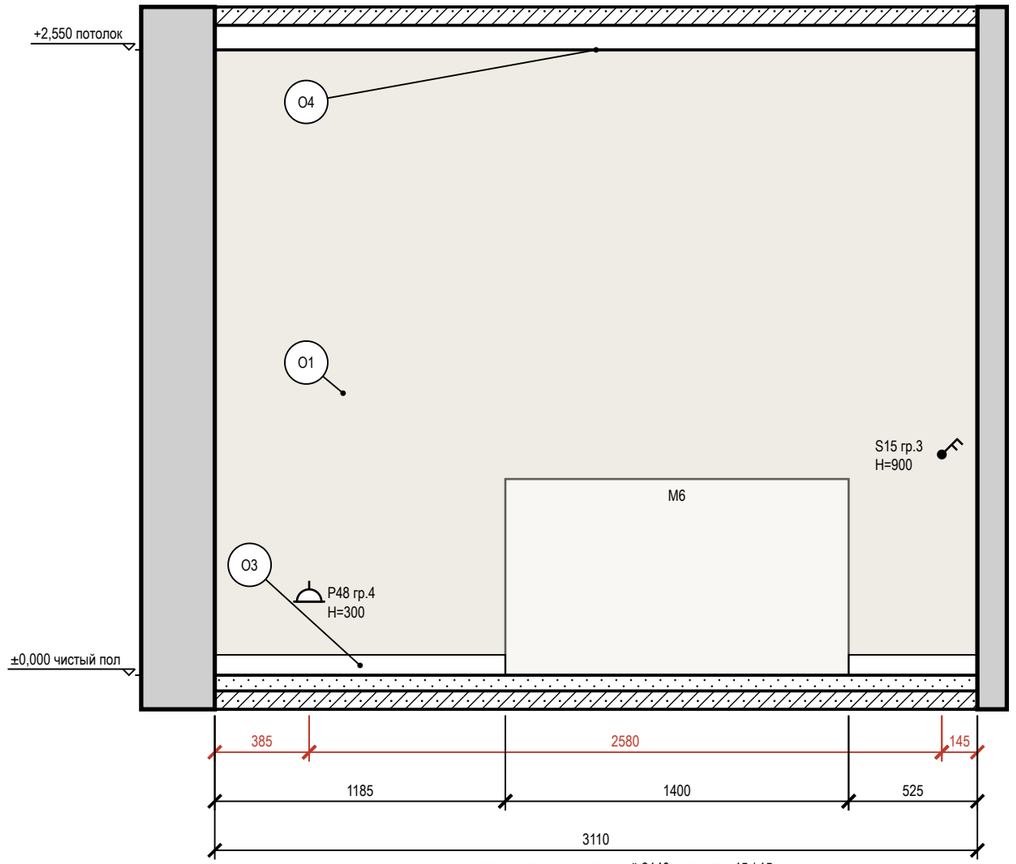


между чистовыми гранями: черновой 3140 − отделка 15 / 15

Развёртка стены Г1

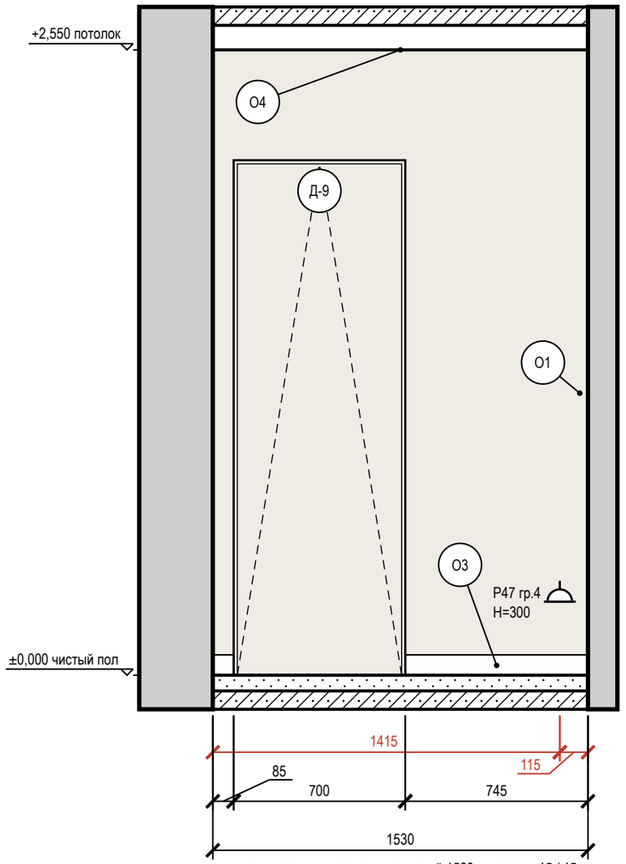

между чистовыми гранями: черновой 1560 − отделка 15 / 15

Схема развёрток (М 1:100)

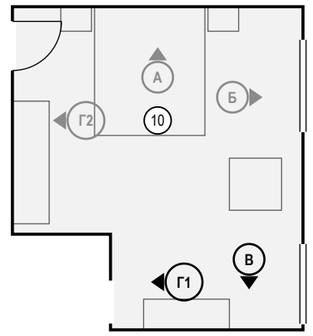

Условные обозначения

- розетка с заземляющим контактом; у знака — марка, ×N постов в рамке, гр. — группа щита, Н — высота оси, мм
- выключатель одноклавишный
- выключатель двухклавишный (флажков — по числу клавиш)
- привязки точек и выводов от угла и от пола, мм
- мебель и приборы — фасад по расстановке (условно)
- дверь скрытого монтажа: полотно в плоскости стены (узел — на листе узлов)
- стены и перекрытия в сечении
- окраска: тон — цвет по коду производителя (условно)
- О1 — марка отделки по реестру отделки альбома
- А — марка развёртки: буква стены, стрелка — взгляд

Ведомость отделки (на листе)

Марка	Поверхность	Материал, изделие	Цвет, код	Кол.
О1	стены	окраска, Farrow & Ball Modern Emulsion, матовая, подготовка Q3	Farrow & Ball No. 291 «School House White тёплый меловой белый»	10,4 м²
О3	плинтус	плинтус МДФ, h 83 мм, Ultrawood Base 5340, ЛДФ под окраску, 83×15 мм, 2440 мм (арт. LDF-BASE-5340)	Farrow & Ball No. 291 «School House White тёплый меловой белый»	2,5 м
О4	потолок	окраска, Tikkurila Anti-Reflex 2, глубокоматовая, подготовка Q3	NCS S 0502-Y «Белый с лёгкой желтизной»	22,5 м²

Примечания

1. Развёртки — вид на стену изнутри помещения, по часовой стрелке; расположение — на схеме листа и на листе 79; размеры — в мм по чистовым поверхностям; отметки — в м от ±0,000; высоты Н — от чистого пола помещения до оси изделия, у декора — до центра.
2. Красная цепочка — привязки электроточек и выводов по осям от угла чистовых стен; высота Н — у знака, от чистого пола до оси; высоты мебели, проёмов и границ отделки — колонкой отметок слева. Стена с 5 и более точками или с мелкими звеньями привязок показана двумя видами: архитектурная развёртка (мебель, отделка, проёмы, высоты) и вид «Привязки» на отдельном листе — точки и выводы с марками, одна цепочка по осям и таблица привязок (каждая точка — строка).
3. У знака электроточки: марка (Р — розетка, S — выключатель, Св — светильник, ЭВ — вывод кабеля), ×N — число постов в рамке, гр. — группа щита, Н — высота оси от чистого пола, мм; группы по клавишам выключателя — на листе выключателей.
4. Схема мебели, приборов и декора не является технической документацией для производства мебели; габариты — по паспортам изделий.
5. Двери скрытого монтажа — полотно в плоскости стены, отделка стены по полотну, плинтус прерывается у короба (узел — на листе узлов).

1000 мм · печать 1:1

Допущения и предложения на листе

Основа листа: размеры сняты со скана обмерного плана KV design (см): часть подписей не читается, помещения выровнены по читаемым размерам; контрольный обмер не выполнен (К-1); высота потолка 2650 мм принята по отметкам обмера (Н = 2,50…2,66 м, ригель 2,28 м) — уточнить при обмере (К-2); толщины стен 300 / 120 мм приняты, межквартирная стена и колонны — по скану, не замерены (К-1); разрешённая мощность 15 кВт принята по типовым ТУ; при объединении двух квартир — переоформление ТУ (К-4); подрайон климата не задан — принят не северный (жилые от 2,5 м) (К-8).

Знак «*» — принято, не замерено и не подтверждено (замерить на объекте): К-1: окно пом. 10 (стена Б) — Окно 1300 при offset 3500 на стене Б основной части (длина 3830) выходило за стену на 970 мм.

См. лист открытых вопросов (лист 6, записи К-1, К-2, К-4, К-8).

Изм.	Кол.уч	Лист	№ док.	Подп.	Дата
Разраб.		Кырлан А.С.			04.11.26
Пров.					
ГИП					
Н. контр.					
Утв.					

ГД-2026-009-АИ

Квартира 103 м²

Общая площадь 100,72* м² · * размеры со скана, не замерены (реестр — л. 6, 7, К-1)

Дизайн-проект интерьера	Стадия	Лист	Листов
	РП	108	120

Развёртки стен В, Г1. Спальня мастер (пом. 10)

М 1:25

Кырлан Александр Сергеевич

выпуск 04.11.2026 № 20cec94f32 · стр. 117 из 130

Развёртка стены Г2. Спальня мастер (пом. 10)

Спальня мастер (пом. 10) · вид изнутри помещения · размеры в мм, отметки в м

ПРЕДВАРИТЕЛЬНО · не для производства работ · открыто пунктов: 8 (реестр — л. 6, 7)

Развёртка стены Г2


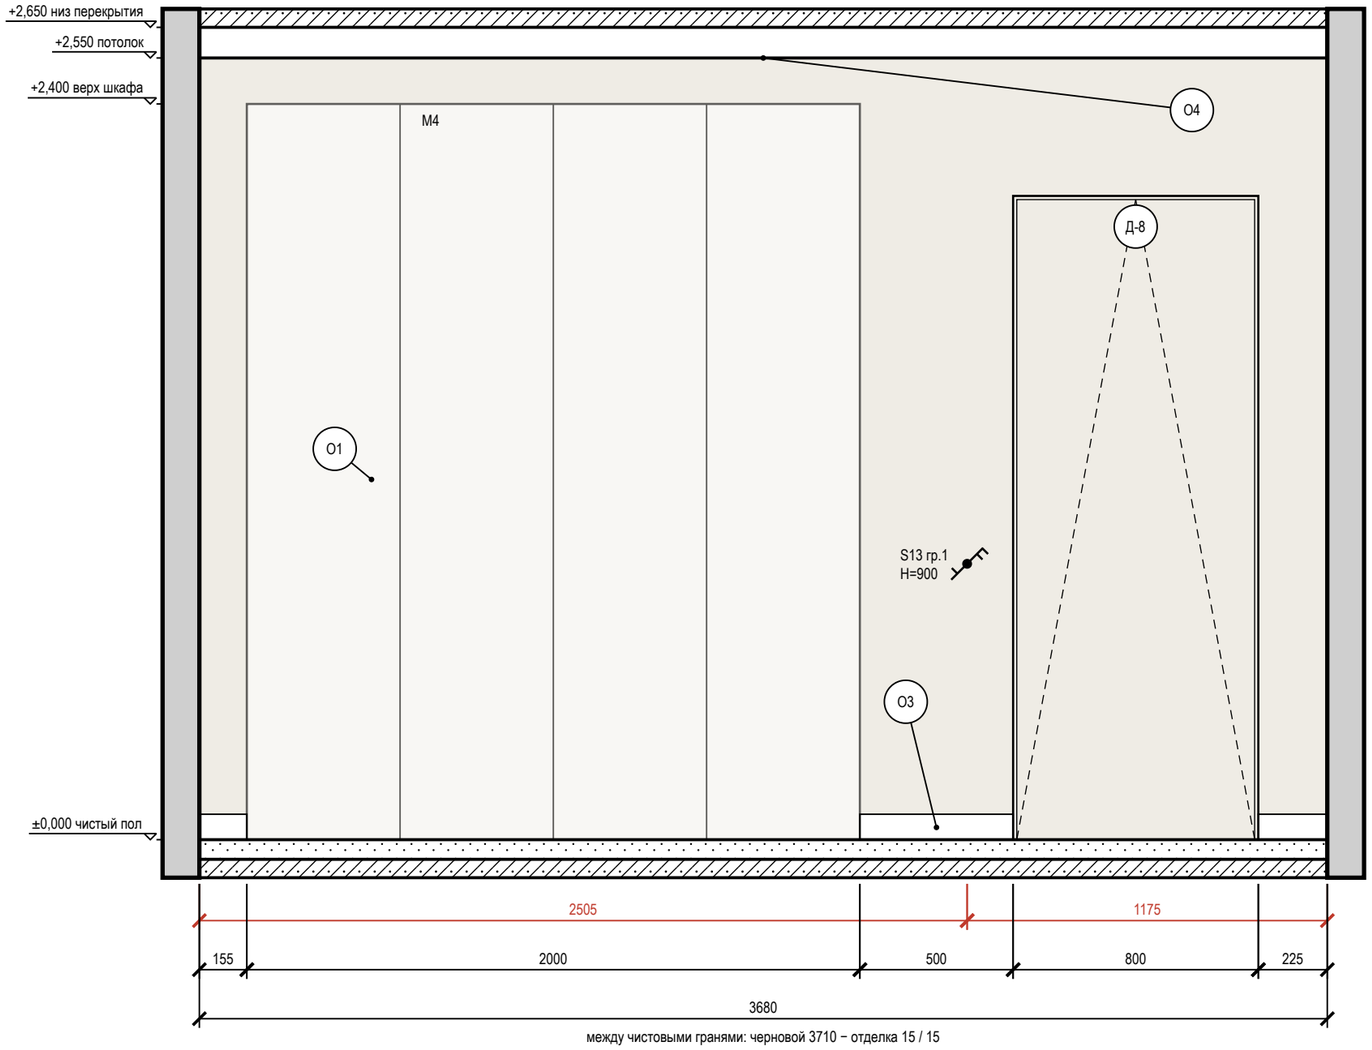


Схема развёрток (М 1:100)

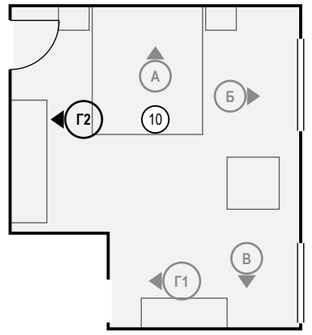

Условные обозначения

- выключатель одноклавишный
- выключатель двухклавишный (флажков — по числу клавиш)
- выключатель с проходной или перекрёстной клавишей (обратный флажок); тип клавиши — в подписи
- привязки точек и выводов от угла и от пола, мм
- мебель и приборы — фасад по расстановке (условно)
- дверь скрытого монтажа: полотно в плоскости стены (узел — на листе узлов)
- стены и перекрытия в сечении
- окраска: тон — цвет по коду производителя (условно)
- О1 — марка отделки по реестру отделки альбома
- А — марка развёртки: буква стены, стрелка — взгляд

Ведомость отделки (на листе)

Марка	Поверхность	Материал, изделие	Цвет, код	Кол.
О1	стены	окраска, Farrow & Ball Modern Emulsion, матовая, подготовка Q3	Farrow & Ball No. 291 «School House White — тёплый меловой белый»	7,7 м²
О3	плинтус	плинтус МДФ, h 83 мм, Ultrawood Base 5340, ЛДФ под окраску, 83×15 мм, 2440 мм (арт. LDF-BASE-5340)	Farrow & Ball No. 291 «School House White — тёплый меловой белый»	0,9 м
О4	потолок	окраска, Tikkurila Anti-Reflex 2, глубокоматовая, подготовка Q3	NCS S 0502-Y «Белый с лёгкой желтизной»	22,5 м²

Допущения и предложения на листе

Основа листа: размеры сняты со скана обмерного плана KV design (см): часть подписей не читается, помещения выровнены по читаемым размерам; контрольный обмер не выполнен (К-1); высота потолка 2650 мм принята по отметкам обмера (Н = 2,50…2,66 м, ригель 2,28 м) — уточнить при обмере (К-2); толщины стен 300 / 120 мм приняты, межквартирная стена и колонны — по скану, не замерены (К-1); разрешённая мощность 15 кВт принята по типовым ТУ; при объединении двух квартир — переоформление ТУ (К-4); подрайон климата не задан — принят не северный (жилые от 2,5 м) (К-8).

Знак «*» — принято, не замерено и не подтверждено (замерить на объекте): К-1: окно пом. 10 (стена Б) — Окно 1300 при offset 3500 на стене Б основной части (длина 3830) выходило за стену на 970 мм.

См. лист открытых вопросов (лист 6, записи К-1, К-2, К-4, К-8).

Примечания

1. Развёртки — вид на стену изнутри помещения, по часовой стрелке; расположение — на схеме листа и на листе 79; размеры — в мм по чистовым поверхностям; отметки — в м от ±0,000; высоты Н — от чистого пола помещения до оси изделия, у декора — до центра.
2. Красная цепочка — привязки электроточек и выводов по осям от угла чистовых стен; высота Н — у знака, от чистого пола до оси; высоты мебели, проёмов и границ отделки — колонкой отметок слева. Стена с 5 и более точками или с мелкими звеньями привязок показана двумя видами: архитектурная развёртка (мебель, отделка, проёмы, высоты) и вид «Привязки» на отдельном листе — точки и выводы с марками, одна цепочка по осям и таблица привязок (каждая точка — строка).
3. У знака электроточки: марка (Р — розетка, S — выключатель, Св — светильник, ЭВ — вывод кабеля), ×N — число постов в рамке, гр. — группа щита, Н — высота оси от чистого пола, мм; группы по клавишам выключателя — на листе выключателей.
4. Схема мебели, приборов и декора не является технической документацией для производства мебели; габариты — по паспортам изделий.
5. Двери скрытого монтажа — полотно в плоскости стены, отделка стены по полотну, плинтус прерывается у короба (узел — на листе узлов).

1000 мм · печать 1:1

Изм.	Кол.уч	Лист	№ док.	Подп.	Дата	ГД-2026-009-АИ			
						Квартира 103 м²			
						Общая площадь 100,72* м² · * размеры со скана, не замерены (реестр — л. 6, 7, К-1)			
Разраб.		Кырлан А.С.			04.11.26	Дизайн-проект интерьера	Стадия	Лист	Листов
Пров.							РП	109	120
ГИП									
Н. контр.						Развёртка стены Г2. Спальня мастер (пом. 10) М 1:20	Кырлан Александр Сергеевич		
Утв.									


выпуск 04.11.2026 № 20cec94f32 · стр. 118 из 130

Развёртки стен А, Б, В. Ванная мастер (пом. 11)

Ванная мастер (пом. 11) · вид изнутри помещения · размеры в мм, отметки в м


ПРЕДВАРИТЕЛЬНО · не для производства работ · открыто пунктов: 8 (реестр — л. 6, 7)

Развёртка стены А

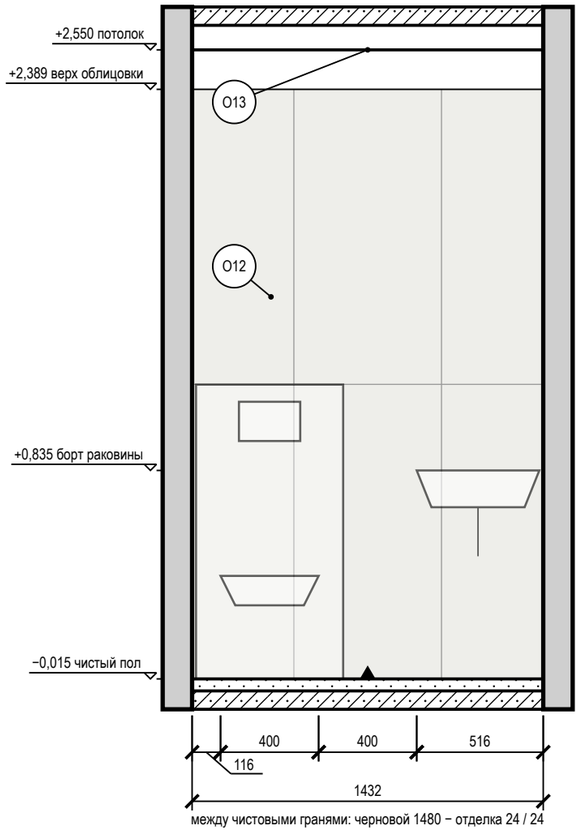


между чистовыми гранями: черновой 1480 − отделка 24 / 24

Развёртка стены Б

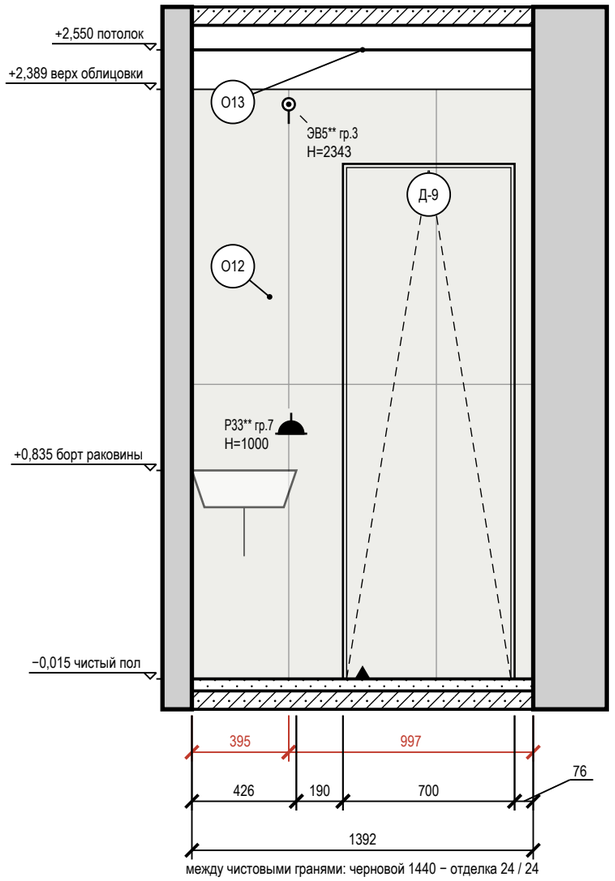


между чистовыми гранями: черновой 1440 − отделка 24 / 24

Развёртка стены В

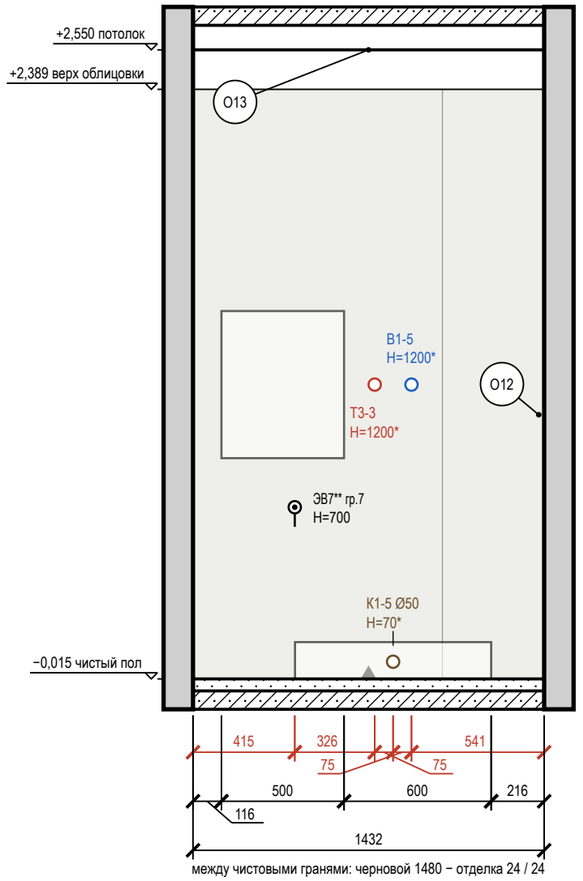

между чистовыми гранями: черновой 1480 − отделка 24 / 24

Схема развёрток (М 1:100)

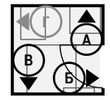

Допущения и предложения на листе

Основа листа: размеры сняты со скана обмерного плана KV design (см): часть подписей не читается, помещения выровнены по читаемым размерам; контрольный обмер не выполнен (К-1); высота потолка 2650 мм принята по отметкам обмера (Н = 2,50…2,66 м, ригель 2,28 м) — уточнить при обмере (К-2); толщины стен 300 / 120 мм приняты, межквартирная стена и колонны — по скану, не замерены (К-1); разрешённая мощность 15 кВт принята по типовым ТУ; при объединении двух квартир — переоформление ТУ (К-4); подрайон климата не задан — принят не северный (жилые от 2,5 м) (К-8).

Знак «**» — предложение проектировщика, заказчиком не утверждено (согласовать с заказчиком): ЭВ5 — по образцу: Добавлены выводы к вентиляторам: ЭВ4 (ВР1, ванная) и ЭВ5 (ВР3, санузел 2) — группа 3, высота 2389 мм, включение с основным светом, таймер выбега в вентиляторе; и коробки уравнивания потенциалов КУП1 (ванная) и КУП2 (санузел 2) — высота 300 мм, у входа, вне зон 0–2, проводник от шины PE щита ЩК …; сдвиг под раскладку плитки стены Б на 29 мм вдоль стены и на 46 мм ниже — ось на шве или в центре плитки, привязка по таблице листа; ИЗ-1: Р33 — по образцу: Розетка Р33 на высоте 1100 мм, вне шва плитки; ЭВ7 — по образцу: Добавлены электрические полотенцесушители IP44: П10 в ванной (480 мм, низ 900 мм) и П13 в санузле 2 (400 мм, низ 900 мм), выводы ЭВ6 и ЭВ7; мощность группы 13 — 2,4 кВт вместо 1,8 кВт; сдвиг под раскладку плитки стены В на 101 мм вдоль стены — ось на шве или в центре плитки, привязка по таблице листа.

См. лист открытых вопросов (лист 6, записи ИЗ-1, К-1, К-2, К-4, К-8).

Условные обозначения

- розетка влагозащищённая IP44
- вывод кабеля для подключения прибора (без розетки), марка ЭВ
- вывод В1 (код — в ведомости привязок)
- вывод Т3 (код — в ведомости привязок)
- вывод К1 (код — в ведомости привязок)
- привязки точек и выводов от угла и от пола, мм
- мебель и приборы — фасад по расстановке (условно)
- дверь скрытого монтажа: полотно в плоскости стены (узел — на листе узлов)
- стены и перекрытия в сечении
- плитка: сетка швов по формату, ▲ — ось старта
- О1 — марка отделки по реестру отделки альбома
- А — марка развёртки: буква стены, стрелка — взгляд

Примечания

1. Развёртки — вид на стену изнутри помещения, по часовой стрелке; расположение — на схеме листа и на листе 79; размеры — в мм по чистовым поверхностям; отметки — в м от ±0,000; высоты Н — от чистого пола помещения до оси изделия, у декора — до центра.
2. Красная цепочка — привязки электроточек и выводов по осям от угла чистовых стен; высота Н — у знака, от чистого пола до оси; высоты мебели, проёмов и границ отделки — колонкой отметок слева. Стена с 5 и более точками или с мелкими звеньями привязок показана двумя видами: архитектурная развёртка (мебель, отделка, проёмы, высоты) и вид «Привязки» на отдельном листе — точки и выводы с марками, одна цепочка по осям и таблица привязок (каждая точка — строка).
3. Стена А показана двумя видами: здесь — архитектурная развёртка (мебель, отделка, проёмы, высоты), электроточки и выводы ВК с привязками и таблицей — на листе 111 («Привязки»).
4. У знака электроточки: марка (Р — розетка, S — выключатель, Св — светильник, ЭВ — вывод кабеля), ×N — число постов в рамке, гр. — группа щита, Н — высота оси от чистого пола, мм; группы по клавишам выключателя — на листе выключателей.
5. Схема мебели, приборов и декора не является технической документацией для производства мебели; габариты — по паспортам изделий (* — высота не задана в проекте, показана по типовому изделию).
6. Выводы ВК — коды и высоты по листу выводов сантехники; * — высота принята по типовой практике монтажа, окончательно — по паспорту прибора.
7. Облицовка — по сетке швов 2 мм, раскладка от оси стены (треугольник у пола), целые ряды от пола; подрезки — по листу раскладки плитки.
8. Гидроизоляция в 2 слоя, заход на стены 200 мм; у душа — до 2000 и 500 мм за поддон — до облицовки, с актом скрытых работ и тестом проливом (узел — на листе узлов).
9. Двери скрытого монтажа — полотно в плоскости стены, отделка стены по полотну, плинтус прерывается у короба (узел — на листе узлов).
10. Линии узора (швы плитки, складки штор, рёбра радиаторов) прерываются у знаков и выносок — просвет между линиями не менее 0,7 мм.

1000 мм · печать 1:1

Ведомость отделки (на листе)

Марка	Поверхность	Материал, изделие	Цвет, код	Кол.
О12	стены	облицовка плиткой, Atlas Concorde Marvel Travertine, 600×1200×9 мм, A8UZ, затирка CG2WA	Atlas Concorde A8UZ «Marvel Travertine»	8,8 м²
О13	потолок	окраска, Tikkurila Luja 7, матовая, подготовка Q3	NCS S 0502-Y «Белый с лёгкой желтизной»	2,1 м²

Изм.	Кол.уч	Лист	№ док.	Подп.	Дата			
Разраб.		Кырлан А.С.			04.11.26	**ГД-2026-009-АИ**		
Пров.						Квартира 103 м²		
ГИП						Общая площадь 100,72* м² · * размеры со скана, не замерены (реестр — л. 6, 7, К-1)		
						Дизайн-проект интерьера	Стадия: РП; Лист: 110; Листов: 120	
Н. контр.						**Развёртки стен А, Б, В. Ванная мастер (пом. 11)** М 1:25	**Кырлан Александр Сергеевич**	
Утв.								

выпуск 04.11.2026 № 20cec94f32 · стр. 119 из 130

Привязки электроточек и выводов ВК, стена А. Ванная мастер (пом. 11)

Ванная мастер (пом. 11) · вид изнутри помещения · привязки в мм, отметки в м · к развёртке на листе 110

Развёртка стены А: электроточки и выводы

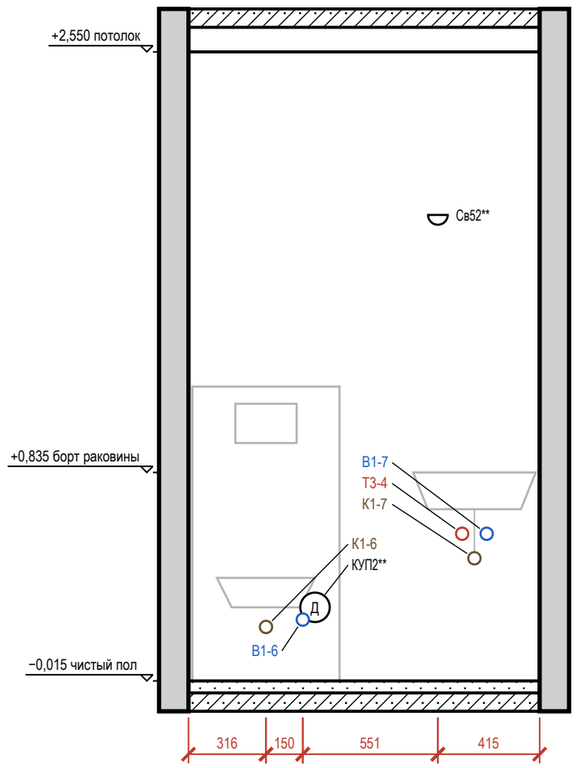



Таблица привязок электроточек и выводов

Марка	Назначение	От угла, мм	Н от пола, мм	Примечание
К1-6	канализация — унитаз подвесной	316	220*	Ø110
В1-6	холодная вода — унитаз подвесной	466	250*	в раме инсталляции
КУП2**	КУП — уравнивание потенциалов (ДСУП)	516	300	
Св52**	светильник настенный	1017	1900	гр. 3
Т3-4	горячая вода — умывальник	1116	600*	межос. 100
К1-7	канализация — умывальник	1166	500*	Ø50
В1-7	холодная вода — умывальник	1216	600*	межос. 100

Условные обозначения

- светильник настенный (бра), Н — высота оси
- вывод В1 (код — в ведомости привязок)
- вывод Т3 (код — в ведомости привязок)
- вывод К1 (код — в ведомости привязок)
- привязки точек и выводов от угла и от пола, мм
- А — марка развёртки: буква стены, стрелка — взгляд

Схема развёрток (М 1:50)

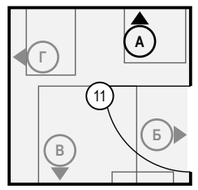

Примечания

1. Вид «Привязки» стены А — электроточки и выводы ВК; архитектурная развёртка (мебель, отделка, проёмы, высоты) — на листе 110, расположение — на листе 79. Мебель и приборы — подложкой для ориентира; их марки и обозначения мебели, проёмов и стен — там же.
2. Привязки — в мм: по горизонтали от левого чистового угла стены до оси изделия, Н — от чистого пола до оси; все точки — в таблице привязок. Красная цепочка — привязки по осям; точки ближе 150 мм одна к другой в цепочку не дробятся — их привязки только в таблице.
3. У знака — марка электроточки (Р — розетка, S — выключатель, Св — светильник, ЭВ — вывод кабеля); посты в рамке и группа щита — в графе «Примечание»; группы по клавишам выключателя — на листе выключателей.
4. Коды выводов ВК: В1 — холодная вода, Т3 — горячая вода, К1 — канализация; номер после дефиса — номер вывода на листе выводов сантехники; * — высота принята по типовой практике монтажа, окончательно — по паспорту прибора.

Допущения и предложения на листе

Основа листа: размеры сняты со скана обмерного плана KV design (см): часть подписей не читается, помещения выровнены по читаемым размерам; контрольный обмер не выполнен (К-1); высота потолка 2650 мм принята по отметкам обмера (Н = 2,50…2,66 м, ригель 2,28 м) — уточнить при обмере (К-2); толщины стен 300 / 120 мм приняты, межквартирная стена и колонны — по скану, не замерены (К-1); разрешённая мощность 15 кВт принята по типовым ТУ; при объединении двух квартир — переоформление ТУ (К-4); подрайон климата не задан — принят не северный (жилые от 2,5 м) (К-8).

Знак «**» — предложение проектировщика, заказчиком не утверждено (согласовать с заказчиком): Св52 — свет у зеркала — над зеркалом у умывальника по его оси (свет на лицо, а не над сантехникой); сдвиг под раскладку плитки стены А на 149 мм вдоль стены — ось на шве или в центре плитки, привязка по таблице листа; КУП2 — по образцу: Добавлены выводы к вентиляторам: ЭВ4 (ВР1, ванная) и ЭВ5 (ВР3, санузел 2) — группа 3, высота 2389 мм, включение с основным светом, таймер выбега в вентиляторе; и коробки уравнивания потенциалов КУП1 (ванная) и КУП2 (санузел 2) — высота 300 мм, у входа, вне зон 0–2, проводник от шины PE щита ЩК ….

См. лист открытых вопросов (лист 6, записи К-1, К-2, К-4, К-8).

1000 мм · печать 1:1

Изм.	Кол.уч	Лист	№ док.	Подп.	Дата
Разраб.		Кырлан А.С.			04.11.26
Пров.					
ГИП					
Н. контр.					
Утв.					

ГД-2026-009-АИ

Квартира 103 м²

Общая площадь 100,72* м² · * размеры со скана, не замерены (реестр — л. 6, 7, К-1)

Дизайн-проект интерьера

Стадия	Лист	Листов
РП	111	120

Привязки электроточек и выводов ВК, стена А.
Ванная мастер (пом. 11)
М 1:25

Кырлан Александр Сергеевич

выпуск 04.11.2026 № 20cec94f32 · стр. 120 из 130

Развёртка стены Г. Ванная мастер (пом. 11)

Ванная мастер (пом. 11) · вид изнутри помещения · размеры в мм, отметки в м

ПРЕДВАРИТЕЛЬНО · не для производства работ · открыто пунктов: 8 (реестр — л. 6, 7)

Развёртка стены Г

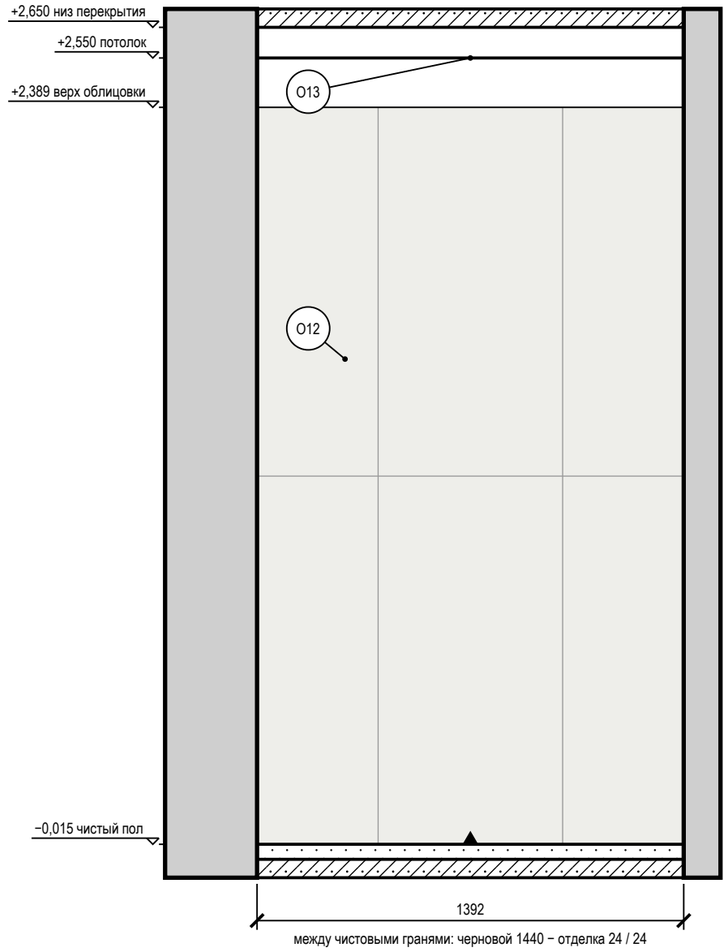


Схема развёрток (М 1:100)



Условные обозначения

- мебель и приборы — фасад по расстановке (условно)
- стены и перекрытия в сечении
- плитка: сетка швов по формату, ▲ — ось старта
- О1 — марка отделки по реестру отделки альбома
- А — марка развёртки: буква стены, стрелка — взгляд

Ведомость отделки (на листе)

Марка	Поверхность	Материал, изделие	Цвет, код	Кол.
О12	стены	облицовка плиткой, Atlas Concorde Marvel Travertine, 600×1200×9 мм, A8UZ, затирка CG2WA	Atlas Concorde A8UZ «Marvel Travertine»	3,3 м²
О13	потолок	окраска, Tikkurila Luja 7, матовая, подготовка Q3	NCS S 0502-Y «Белый с лёгкой желтизной»	2,1 м²

Примечания

1. Развёртки — вид на стену изнутри помещения, по часовой стрелке; расположение — на схеме листа и на листе 79; размеры — в мм по чистовым поверхностям; отметки — в м от ±0,000; высоты Н — от чистого пола помещения до оси изделия, у декора — до центра.
2. Схема мебели, приборов и декора не является технической документацией для производства мебели; габариты — по паспортам изделий.
3. Облицовка — по сетке швов 2 мм, раскладка от оси стены (треугольник у пола), целые ряды от пола; подрезки — по листу раскладки плитки.
4. Гидроизоляция в 2 слоя, заход на стены 200 мм; у душа — до 2000 и 500 мм за поддон — до облицовки, с актом скрытых работ и тестом проливом (узел — на листе узлов).

Допущения и предложения на листе

Основа листа: размеры сняты со скана обмерного плана KV design (см): часть подписей не читается, помещения выровнены по читаемым размерам; контрольный обмер не выполнен (К-1); высота потолка 2650 мм принята по отметкам обмера (Н = 2,50…2,66 м, ригель 2,28 м) — уточнить при обмере (К-2); толщины стен 300 / 120 мм приняты, межквартирная стена и колонны — по скану, не замерены (К-1); разрешённая мощность 15 кВт принята по типовым ТУ; при объединении двух квартир — переоформление ТУ (К-4); подрайон климата не задан — принят не северный (жилые от 2,5 м) (К-8).
См. лист открытых вопросов (лист 6, записи К-1, К-2, К-4, К-8).

1000 мм · печать 1:1

Изм.	Кол.уч	Лист	№ док.	Подп.	Дата
Разраб.		Кырлан А.С.			04.11.26
Пров.					
ГИП					
Н. контр.					
Утв.					

ГД-2026-009-АИ

Квартира 103 м²

Общая площадь 100,72* м² · * размеры со скана, не замерены (реестр — л. 6, 7, К-1)

Дизайн-проект интерьера

Стадия	Лист	Листов
РП	112	120

Развёртка стены Г. Ванная мастер (пом. 11)

М 1:20

Кырлан Александр Сергеевич


выпуск 04.11.2026 № 20cec94f32 · стр. 121 из 130

Узлы

Пороги и стыки покрытий, скрытые двери, короба стояков, гидроизоляция, плинтус


1 Порог 15 мм: мокрая зона — смежное помещение (М 1:10)

Применение: двери Д-5, Д-9; места — лист 79

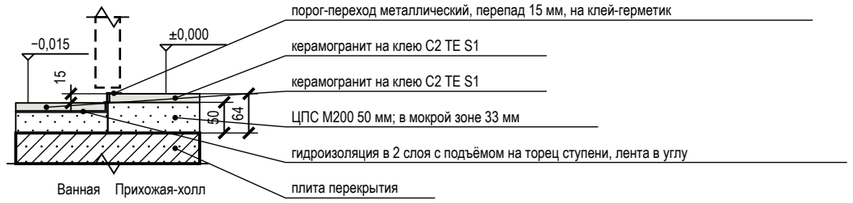


2 Дверь скрытого монтажа в плоскости стены, плинтус (М 1:5)

Применение: двери Д-2, Д-3, Д-4, Д-5, Д-6, Д-7, Д-8, Д-9; места — лист 79

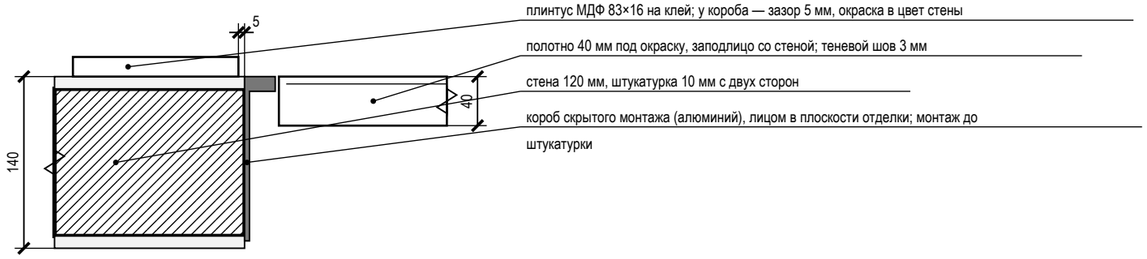


3 Короб стояков К1-1, К1-2 (кухня) с люком и звукоизоляцией (М 1:10)

Применение: пом. 6, 5, 11, 7; места — лист 79

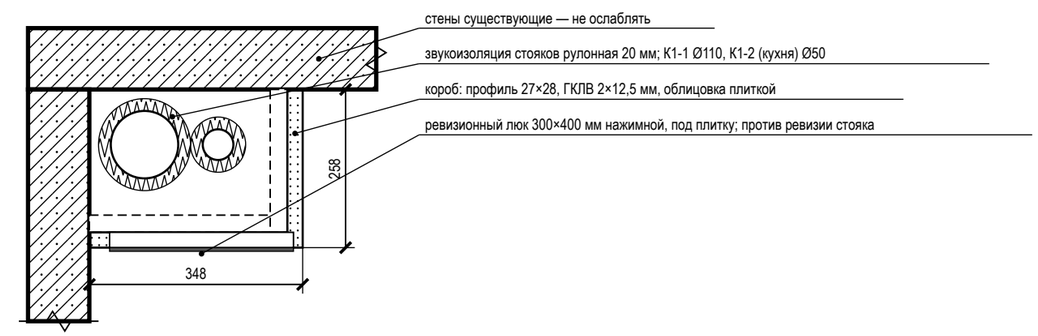


4 Гидроизоляция санузла: заход на стены 200 мм, примыкание ванны (М 1:20)

Применение: пом. 6, 11; места — лист 79

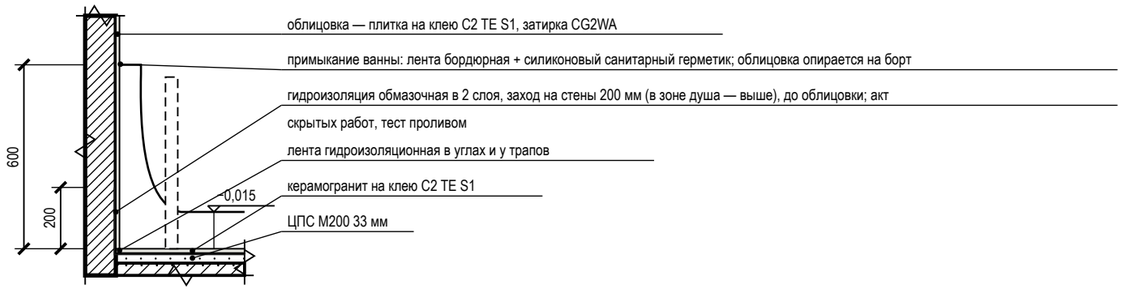


5 Плинтус МДФ 83×15 мм у окрашенной стены по доске (ламинату) (М 1:10)

Применение: пом. 1, 2, 3, 5, 7, 8, 9, 10; места — лист 79

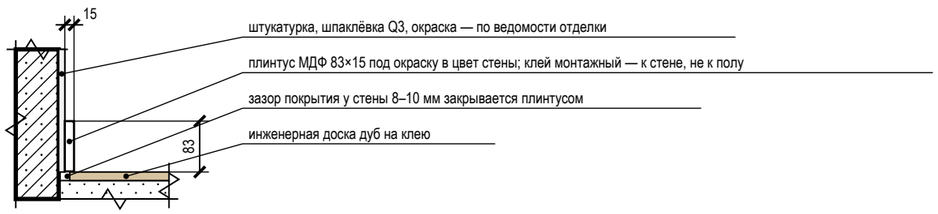

6 Плинтус МДФ 83×15 мм у окрашенной стены по керамограниту (плитке) (М 1:10)

Применение: пом. 4; места — лист 79

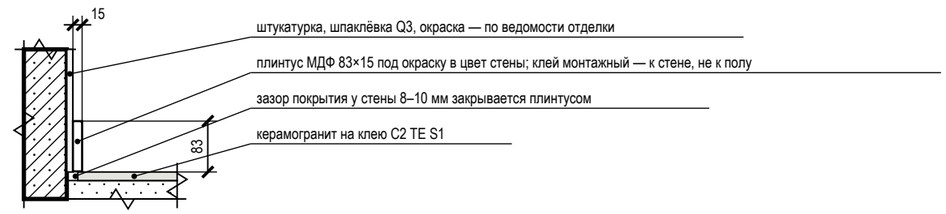

Условные обозначения

- железобетон (плита, стены) — условно: конструкция не установлена
- кладка, перегородка — условно: конструкция не установлена
- стяжка, раствор
- гипсокартон ГКЛВ
- звукоизоляция, эластичный заполнитель
- плитка, керамогранит на клею
- инженерная доска (покрытие пола)
- металлический профиль (порог, Т-профиль, короб двери)
- гидроизоляция (обмазочная, лента)

Примечания

1. Узлы — типовые решения проекта для мест, отмеченных выносками на листе схемы расположения развёрток и узлов; размеры — в мм, отметки — в м от ±0,000.
2. Узлы с гидроизоляцией, закладными и коробами скрытого монтажа принимаются по актам скрытых работ до закрытия отделкой; гидроизоляция — после теста проливом (24 ч).
3. Марки изделий (порог, Т-профиль, короб скрытой двери, люк) — по спецификациям; замена — на аналог с теми же габаритами по согласованию с автором проекта.
4. Материал плиты перекрытия и стен в узлах показан условно (железобетон, кладка): конструкция дома не установлена — крепёж, анкеры и толщины слоёв уточняются после обследования (до него — по допущениям общих указаний).

Допущения и предложения на листе. Основа листа: размеры сняты со скана обмерного плана KV design (см): часть подписей не читается, помещения выровнены по читаемым размерам; контрольный обмер не выполнен (К-1); высота потолка 2650 мм принята по отметкам обмера (Н = 2,50…2,66 м, ригель 2,28 м) — уточнить при обмере (К-2); толщины стен 300 / 120 мм приняты, межквартирная стена и колонны — по скану, не замерены (К-1); разрешённая мощность 15 кВт принята по типовым ТУ; при объединении двух квартир — переоформление ТУ (К-4); подрайон климата не задан — принят не северный (жилые от 2,5 м) (К-8). См. лист открытых вопросов (лист 6, записи К-1, К-2, К-4, К-8).

Изм.	Кол.уч	Лист	№ док.	Подп.	Дата
Разраб.		Кырлан А.С.			04.11.26
Пров.					
ГИП					
Н. контр.					
Утв.					

ГД-2026-009-АИ

Квартира 103 м²

Общая площадь 100,72* м² · * размеры со скана, не замерены (реестр — л. 6, 7, К-1)

Дизайн-проект интерьера

Стадия	Лист	Листов
РП	113	120

Узлы

М 1:10; 1:5; 1:20

Кырлан Александр Сергеевич

выпуск 04.11.2026 № 20cec94f32 · стр. 122 из 130

10

Смета

Кырлан Александр Сергеевич

выпуск 04.11.2026 № 20cec94f32 · стр. 123 из 130

Ведомость объёмов работ

ПРЕДВАРИТЕЛЬНО · не для производства работ · открыто пунктов: 8 (реестр — л. 6, 7)

Объёмы по помещениям от чертежа · площади в м², длины в м · формула, правило проёмов и источник в каждой строке

Ведомость объёмов работ по помещениям

Поз.	Наименование работ (материал, число слоёв)	Ед. изм.	Объём по помещениям (№ по экспликации)											Всего	Формула подсчёта	Правило проёмов	Источник	Цена за ед., ₽	Стоимость, ₽
			1	2	3	4	5	6	7	8	9	10	11						
1. Демонтаж и черновые работы																			
1	Демонтаж существующего покрытия пола до основания	м²	10,57	2,93	20,32	12,91	6,52	3,91	1,51	11,42	6,02	22,48	2,13	100,72	S пом.		л. 14, 15	по КП	
2	Демонтаж существующей отделки стен до основания	м²	31,33	17,61	35,31	33,88	22,52	19,31	11,89	32,98	29,17	43,57	13,51	291,08	P × H − проёмы	за вычетом проёмов	л. 14, 15	по КП	
3	Демонтаж существующей отделки потолка до основания	м²	10,57	2,93	20,32	12,91	6,52	3,91	1,51	11,42	6,02	22,48	2,13	100,72	S пом.		л. 14, 15	по КП	
4	Демонтаж существующих дверных блоков	шт	1	1		1	1	1	1	1		1	1	9	по ведомости проёмов		л. 15–17	по КП	
5	Демонтаж существующих сантехприборов и электрооборудования (если есть)	компл													по факту на объекте		л. 15	по КП	
6	Устройство стяжки: стяжка ЦПС М200, 50 мм	м²	10,62	2,97	20,55	13,22	6,57	3,95	1,55	11,46	6,22	22,57	2,17	101,85	S пом. + S в дверных проёмах (b × t/2)	проёмы добавлены	л. 53–56	530	53 981
7	Гидроизоляция обмазочная, 2 слоя: пол, стены на 200 мм, зоны замачивания	м²						11,45					5,56	17,01	пол + (P − двери) × h заведения + зоны замачивания		л. 49	450	7 655
8	Штукатурка стен по маякам, до 10 мм	м²	31,33	17,61	35,31	33,88	22,52	19,31	11,89	32,98	29,17	43,57	13,51	291,08	P × H − проёмы по обводу коробок − грани перегородок на ГКЛВ	за вычетом проёмов	л. 14, 54–56	530	154 272
9	Штукатурка оконных откосов шириной более 200 мм	м²	0,99		2,02		0,99			1,01		2,07		7,08	Σ (2h + b) × глубина откоса	откосы > 200 мм	л. 14	540	3 823
10	Потолок ГКЛ по каркасу П113, 1 слой	м²	10,57		20,32	12,91	6,52	3,91		11,42	6,02	22,48	2,13	96,28	S пом. по плану потолков		л. 45–48	1 500	144 420
Итого по разделу 1 — 364 151 ₽ (позиций 10, из них по КП 5); в сводную смету — л. 119, 120																			
2. Инженерные системы																			
11	Прокладка кабеля ВВГнг(A)-LS по группам щита: за потолком и в штробах стен (штробы — только после технического заключения, см. строку «Штробы в стенах»)	м												595,50	Σ длин групп щита		л. 28	60	35 730
12	Прокладка слаботочной линии: Кабель домофона — тип по системе поставщика, отдельно от силовых	м												4,30	по лучам от ЩС**: 1 точ., запас 10 %		л. 30	по КП	
13	Прокладка слаботочной линии: Кабель коаксиальный RG-6 (75 Ом) к розеткам ТВ, отдельно от силовых	м												16,10	по лучам от ЩС**: 1 точ., запас 10 %		л. 30	по КП	
14	Прокладка слаботочной линии: Кабель U/UTP кат. 6 (LAN, Wi-Fi и камеры по PoE), отдельно от силовых	м												70,30	по лучам от ЩС**: 5 точ., запас 10 %		л. 30	по КП	
15	Прокладка гофротрубы Ø20 для слаботочных линий, отдельно от силовых	м												81,60	по длине лучей без участков в канале плинтуса (≈ 90 %)		л. 30	по КП	
16	Сборка слаботочного щита ЩС**: корпус, патч-панель, подключение линий и питания 220 В; коммутатор и точки доступа — оборудование заказчика	шт												1	один щит		л. 26, 27, 30	по КП	
17	Электроточка: подрозетник в бетоне, розетка, выключатель, вывод	шт	6	1	10	8	10	3	2	8	2	9	3	62	по ведомости электроточек		л. 23, 26, 27	950	58 900
18	Штробы в стенах под спуски кабеля к точкам — выполняются только после технического заключения о несущих стенах	м	8,40	1,75	18,40	11,35	15,70	3,59	3,40	16,00	3,90	17,45	3,65	103,59	Σ (H − h) по точкам на стенах: вертикальные спуски	после техзаключения	л. 15, 23	по КП	
19	Установка встраиваемого точечного светильника	шт	6		8	4	7	3		6	2	8	2	46	по плану освещения		л. 24	750	34 500
20	Монтаж светильника: потолочного, подвесного, настенного	шт		1	1			1	1	1		2	1	8	по плану освещения		л. 24	1 200	9 600
21	Монтаж LED-ленты в алюминиевый профиль	м	12,30		5,40	1,80	1,20			12,30		15,50		48,50	Σ длин лент по плану освещения		л. 24	230	11 155
22	Установка блока питания LED в доступном месте (люк, шкаф)	шт	1		1	1	1			1		1		6	один на LED-группу		л. 24	570	3 420
23	Установка автономного пожарного извещателя	шт	1		1	1	1			1	1	1		7	по плану розеток		л. 23	по КП	

Допущения и предложения на листе

Основа листа: размеры сняты со скана обмерного плана KV design (см): часть подписей не читается, помещения выровнены по читаемым размерам; контрольный обмер не выполнен (К-1); высота потолка 2650 мм принята по отметкам обмера (H = 2,50…2,66 м, ригель 2,28 м) — уточнить при обмере (К-2); толщины стен 300 / 120 мм приняты, межквартирная стена и колонны — по скану, не замерены (К-1); разрешённая мощность 15 кВт принята по типовым ТУ; при объединении двух квартир — переоформление ТУ (К-4); подрайон климата не задан — принят не северный (жилые от 2,5 м) (К-8).

Знак «**» — предложение проектировщика, заказчиком не утверждено (согласовать с заказчиком): ЩС — щит слаботочный: место и состав.

См. лист открытых вопросов (лист 6, записи К-1, К-2, К-4, К-8).

Изм.	Кол.уч	Лист	№ док.	Подп.	Дата
Разраб.		Кырлан А.С.			04.11.26
Пров.					
ГИП					
Н. контр.					
Утв.					

ГД-2026-009-АИ

Квартира 103 м²

Общая площадь 100,72* м² · * размеры со скана, не замерены (реестр — л. 6, 7, К-1)

Дизайн-проект интерьера

Стадия	Лист	Листов
РП	114	120

Ведомость объёмов работ

М б/м

Кырлан Александр Сергеевич

Ведомость объёмов работ (продолжение)

Объёмы по помещениям от чертежа · площади в м², длины в м · формула, правило проёмов и источник в каждой строке

Ведомость объёмов работ по помещениям (продолжение)

Поз.	Наименование работ (материал, число слоёв)	Ед. изм.	Объём по помещениям (№ по экспликации)											Всего	Формула подсчёта	Правило проёмов	Источник	Цена за ед., ₽	Стоимость, ₽
			1	2	3	4	5	6	7	8	9	10	11						
24	Сборка щита: установка автоматов и АВДТ групп, вводного автомата	шт												15	группы + вводной автомат		л. 28	230	3 450
25	Установка вводного УЗО	шт												1	по однолинейной схеме		л. 28	380	380
26	Монтаж инсталляции, установка подвесного унитаза и кнопки смыва	шт						1					1	2	по плану выводов		л. 33, 42	10 500	21 000
27	Короб инсталляции: каркас и обшивка ГКЛВ в 2 слоя, ревизионный доступ к смыву	шт						1					1	2	по плану выводов		л. 33, 49–52	по КП	
28	Короб К1 над чистым полом: каркас и обшивка ГКЛВ под плитку (материалы — в спецификации ВК)	м.п.						3,55	0,44				3,08	7,07	Σ открытых участков выпусков К1 (профиль листа разводки ВК)		л. 33, 42	по КП	
29	Установка ванны с сифоном	шт						1						1	по плану выводов		л. 33, 42	6 000	6 000
30	Установка умывальника (мойки) с сифоном и смесителем	шт						1					1	2	по плану выводов		л. 33, 42	3 000	6 000
31	Установка душевого поддона с трапом, ограждения	шт											1	1	по плану выводов		л. 33, 42	по КП	
32	Подключение стиральной (посудомоечной) машины к ВК	шт							1					1	по плану выводов		л. 33	по КП	
33	Установка радиатора с узлом подключения и терморегулятором	шт	1		2		1			1		2		7	по плану отопления		л. 32	по КП	
Итого по разделу 2 — 190 135 ₽ (позиций 23, из них по КП 12); в сводную смету — л. 119, 120																			
3. Чистовые работы																			
34	Облицовка стен керамогранитом 600×1200 на клею	м²						17,04					11,85	28,89	по раскладке: зона облицовки − место за коробом	за вычетом проёмов	л. 49–52	2 500	72 225
35	Облицовка короба инсталляции (ГКЛВ) керамогранитом: лицо, боковины, полка	м²						1,76					1,47	3,23	по раскладке: лицо, боковины, полка		л. 49–52	2 500	8 075
36	Укладка керамогранита на пол, 600×1200, на клею	м²				13,22		3,95					2,17	19,34	S пом. + S в дверных проёмах	проёмы добавлены	л. 49–53	1 800	34 812
37	Затирка швов керамогранита	м²				12,91		22,71					15,45	51,07	Σ S облицовки и пола из плитки		л. 49–52	150	7 661
38	Грунтование стен, 2 слоя (под штукатурку и под отделку)	м²	31,33	17,61	35,31	33,88	22,52	19,31	11,89	32,98	29,17	43,57	13,51	291,08	P × H − проёмы	за вычетом проёмов	л. 54–56	96	27 944
39	Шпаклёвка стен под окраску, 2 слоя (старт и финиш), уровень Q3	м²	31,33	17,61	35,31	33,88	22,52		11,89	32,98	29,17	43,57		258,26	P × H − проёмы − фартук	за вычетом проёмов	л. 54–56	750	193 695
40	Грунтование и шпаклёвка оконных откосов, 2 слоя	м.п.	4,32		8,80		4,30			4,40		8,99		30,81	Σ (2h + b) по окнам	по окнам	л. 14	300	9 243
41	Грунтование потолка, 2 слоя	м²	10,57	2,93	20,32	12,91	6,52	3,91	1,51	11,42	6,02	22,48	2,13	100,72	S пом.		л. 54–56	96	9 669
42	Шпаклёвка потолка под окраску, 2 слоя, уровень Q3	м²	10,57	2,93	20,32	12,91	6,52	3,91	1,51	11,42	6,02	22,48	2,13	100,72	S пом.		л. 45–48, 54–56	950	95 684
43	Окраска потолка водно-дисперсионной краской, 2 слоя	м²	10,57	2,93	20,32	12,91	6,52	3,91	1,51	11,42	6,02	22,48	2,13	100,72	S пом.		л. 54–56	360	36 259
44	Окраска стен водно-дисперсионной краской, 2 слоя	м²	34,88	19,08	47,53	41,57	26,06		13,36	36,47	36,31	51,05		306,31	P × H − фартук, проёмы не вычитаются	без вычета проёмов	л. 54–56	300	91 893
45	Окраска оконных откосов, 2 слоя	м.п.	4,32		8,80		4,30			4,40		8,99		30,81	Σ (2h + b) по окнам	по окнам	л. 14	120	3 697
46	Укладка инженерной доски на клей	м²	10,62	2,97	20,55		6,57		1,55	11,46	6,22	22,57		82,51	S пом. + S в дверных проёмах	проёмы добавлены	л. 53–56	1 200	99 012
47	Установка плинтуса МДФ h=83 мм	м.п.	12,88	6,50	14,74	12,64	9,42		4,34	13,60	10,84	18,52		103,48	P − ширина дверных проёмов		л. 54–56	450	46 566
48	Окраска плинтуса в тоне No. 291, 2 слоя	м.п.	12,88	6,50	14,74	12,64	9,42		4,34	13,60	10,84	18,52		103,48	как плинтус		л. 54–56	300	31 044
49	Монтаж дверей скрытого монтажа под покраску (поставщик дверей)	шт	1	1			1	1	1	1		1	1	8	по ведомости проёмов		л. 16, 17	5 250	42 000
50	Входная дверь, поставка с монтажом и откосами	шт												1	по ведомости проёмов		л. 16, 17	по КП	

Допущения и предложения на листе

Основа листа: размеры сняты со скана обмерного плана KV design (см): часть подписей не читается, помещения выровнены по читаемым размерам; контрольный обмер не выполнен (К-1); высота потолка 2650 мм принята по отметкам обмера (H = 2,50…2,66 м, ригель 2,28 м) — уточнить при обмере (К-2); толщины стен 300 / 120 мм приняты, межквартирная стена и колонны — по скану, не замерены (К-1); разрешённая мощность 15 кВт принята по типовым ТУ; при объединении двух квартир — переоформление ТУ (К-4); подрайон климата не задан — принят не северный (жилые от 2,5 м) (К-8).

См. лист открытых вопросов (лист 6, записи К-1, К-2, К-4, К-8).

Изм.	Кол.уч	Лист	№ док.	Подп.	Дата
Разраб.		Кырлан А.С.			04.11.26
Пров.					
ГИП					
Н. контр.					
Утв.					

ГД-2026-009-АИ

Квартира 103 м²

Общая площадь 100,72* м² · * размеры со скана, не замерены (реестр — л. 6, 7, К-1)

Дизайн-проект интерьера

Стадия	Лист	Листов
РП	115	120

Ведомость объёмов работ (продолжение)

М б/м

Кырлан Александр Сергеевич

Ведомость объёмов работ (окончание)

Объёмы по помещениям от чертежа · площади в м², длины в м · формула, правило проёмов и источник в каждой строке

Ведомость объёмов работ по помещениям (продолжение)

Поз.	Наименование работ (материал, число слоёв)	Ед. изм.	Объём по помещениям (№ по экспликации)											Всего	Формула подсчёта	Правило проёмов	Источник	Цена за ед., ₽	Стоимость, ₽
			1	2	3	4	5	6	7	8	9	10	11						
Итого по разделу 3 — 809 479 ₽ (позиций 17, из них по КП 1); в сводную смету — л. 119, 120																			

Ведомость подсчёта площадей по помещениям

№	Помещение	S пола, м²	P, м	H, м	P × H, м²	Проёмы, м²	Стены нетто, м²	В дверных проёмах, м²	Плинтус, м	Откосы, м.п.
1	Кабинет-библиотека	10,57	13,68	2,55	34,88	3,55	31,33	0,05	12,88	4,32
2	Кладовая	2,93	7,20	2,65	19,08	1,47	17,61	0,04	6,50	нет
3	Гостиная-столовая	20,32	18,64	2,55	47,53	12,22	35,31	0,23	14,74	8,80
4	Прихожая-холл	12,91	16,30	2,55	41,56	7,69	33,88	0,31	12,64	нет
5	Кухня	6,52	10,22	2,55	26,06	3,54	22,52	0,05	9,42	4,30
6	Ванная	3,91	8,10	2,56	20,78	1,47	19,31	0,04	нет	нет
7	Постирочная	1,51	5,04	2,65	13,36	1,47	11,89	0,04	4,34	нет
8	Спальня 2	11,42	14,30	2,55	36,47	3,49	32,98	0,04	13,60	4,40
9	Коридор	6,02	14,24	2,55	36,31	7,14	29,17	0,20	10,84	нет
10	Спальня мастер	22,48	20,02	2,55	51,05	7,48	43,57	0,09	18,52	8,99
11	Ванная мастер	2,13	5,84	2,56	14,98	1,47	13,51	0,04	нет	нет
	Итого	**100,72**			**342,06**	**50,99**	**291,07**	**1,14**	**103,48**	**30,82**

Реестр контрольных сумм

Показатель	По ВОР	По чертежу	Расхождение	Лист
Σ площадей помещений без летних, м² — общая площадь по экспликации	100,72	100,72	0,0 %	л. 14
Стены под окраску, м² (шпаклёвка) ведомость отделки	258,26	258,26	0,0 %	л. 54–56
Потолки под окраску, м² — ведомость отделки	100,72	100,72	0,0 %	л. 54–56
Плинтус, м — ведомость отделки	103,48	103,48	0,0 %	л. 54–56
Плитка к заказу, шт — ведомость плитки	124	124	0,0 %	л. 49
Гидроизоляция, м² — ведомость материалов плитки	17,01	17,01	0,0 %	л. 49
Точки ЭОМ, шт — планы ЭОМ (без щитов)	136	138	-1,4 %	л. 23, 24

Примечания

1. Объёмы — от геометрии проекта (та же, что на планах и в ведомости отделки), не от общей площади: P — периметр чистого контура, H — от чистого пола до низа потолка, проёмы — по наружному обводу коробок.
2. Подсчёт по ГЭСН-2001-15 и ГЭСН-2001-11: штукатурка и шпаклёвка стен — за вычетом проёмов; окраска водными составами — без вычета проёмов (п. 2.24); откосы — отдельно, по ширине до 200 и более 200 мм; полы — с площадью в дверных проёмах.
3. Плитка — по раскладке (целые и с подрезкой); короб инсталляции и фартук — отдельными строками, двойного счёта облицовки нет. Материалы, запас и количество к заказу — в спецификации материалов.
4. Цены — ориентир по открытым прайсам Москвы (цены на 21.09.2026), не коммерческое предложение; «по КП» — расценки нет, строка в итог не входит.
5. Демонтаж — по плану демонтажа и общим указаниям: покрытия пола, отделка стен и потолков, дверные блоки — до основания; объёмы справочные — по плану демонтажа (расценки в книге нет — «по КП»).
6. Штробы в стенах — только после технического заключения о несущих стенах (общие указания, план обмера и демонтажа): строка «Штробы в стенах» вертикальные спуски кабеля от потолочной трассы к точкам, объём не меньше фактического (горизонтальные трассы — по исполнительной схеме). Расценки штробления в прайсе нет — «по КП», в итог не входит; кабель в штробах стен прокладывается после неё.
7. Площадь облицовки стен — одно число с тремя названиями: зона облицовки по ведомости отделки 30,57 м² − место за коробом инсталляции 1,68 м² (плитку туда не кладут) = стены под плитку 28,89 м² (строка «Облицовка стен»); облицовка коробов 3,23 м² — отдельной строкой; стены и короба вместе — 32,12 м² (столько плитки по раскладке в спецификации). Источник — один (quantities.js), расхождение на листах ловит.
8. Слаботочные сети: кабель по лучам от ЩС** 90,70 м (U/UTP, RG-6, домофон — по видам), гофра 81,60 м, щит ЩС** с патч-панелью; розетки RJ45 и ТВ монтируются в строке «Электроточка». Длины те же, что в ведомости изделий электрика (одна модель — lowcurrent-engineer/bom.js); оборудование заказчика (точки доступа, камеры, коммутатор) в спецификацию не входит. 2 точ. — предложение листа слаботочки.
9. Коробы: стояков (нет) и К1 над чистым полом (7,07 м открытых участков; труба К1 вдоль стен 12,85 м в короб не зашивается — она за приборами, в раме инсталляции и в шахтах). В спецификации ВК короб К1 заказывается с запасом 10 % — 7,80 м. Материалы коробов стояков и инсталляции — в спецификации материалов, К1 — в спецификации ВК.

Допущения и предложения на листе

Основа листа: размеры сняты со скана обмерного плана KV design (см): часть подписей не читается, помещения выровнены по читаемым размерам; контрольный обмер не выполнен (К-1); высота потолка 2650 мм принята по отметкам обмера (H = 2,50…2,66 м, ригель 2,28 м) — уточнить при обмере (К-2); толщины стен 300 / 120 мм приняты, межквартирная стена и колонны — по скану, не замерены (К-1); разрешённая мощность 15 кВт принята по типовым ТУ; при объединении двух квартир — переоформление ТУ (К-4); подрайон климата не задан — принят не северный (жилые от 2,5 м) (К-8).

Знак «**» — предложение проектировщика, заказчиком не утверждено (согласовать с заказчиком): ЩС — щит слаботочный: место и состав.

См. лист открытых вопросов (лист 6, записи К-1, К-2, К-4, К-8).

Изм.	Кол.уч	Лист	№ док.	Подп.	Дата				
Разраб.		Кырлан А.С.			04.11.26	ГД-2026-009-АИ			
Пров.						Квартира 103 м²			
ГИП						Общая площадь 100,72* м² · * размеры со скана, не замерены (реестр — л. 6, 7, К-1)			
						Дизайн-проект интерьера	Стадия	Лист	Листов
Н. контр.							РП	116	120
Утв.						Ведомость объёмов работ (окончание) М б/м	Кырлан Александр Сергеевич		

выпуск 04.11.2026 № 20cec94f32 · стр. 126 из 130

Спецификация материалов

Отделочные материалы: чистое количество, запас, упаковка, к заказу · ГОСТ 21.110-2013

ПРЕДВАРИТЕЛЬНО · не для производства работ · открыто пунктов: 8 (реестр — л. 6, 7)

Спецификация материалов (ГОСТ 21.110-2013, форма 1)

Поз.	Наименование и техническая характеристика	Тип, марка, артикул	Код продукции	Поставщик	Ед. изм.	Количество				Масса ед., кг	Примечание
						чистое	запас, %	упаковка	к заказу		
Покрытия полов и облицовка											
1	Инженерная доска (дуб натуральный, рабочий слой 4 мм, эмиссия E1, прямая укладка)	1167-4250			м²	82,52	7	по артикулу	88,30 м²		пом. 1, 2, 3, 5, 7, 8, 9, 10; до целой упаковки; л. 53–56
2	Клей для паркетной и инженерной доски (эластичный, по ТУ изготовителя доски)	по выбору подрядчика			м²	82,52		ведро по ТУ	по ТУ		расход кг/м² — по ТУ клея; л. 53
3	Керамогранит 600×600 мм Atlas Concorde Marvel Travertine Sand Cross 60×60 Matte Sensitech, арт. AFUL (той же коллекции, что стены A8UZ; тон сверить по образцу)	Atlas Concorde Marvel Travertine Sand Cross 60×60 Matte Sensitech, арт. AFUL (той же коллекции, что стены A8UZ; тон сверить по образцу)			шт	23	10	коробка	26 шт		3 целых + 20 с подрезкой; 6,04 м² по раскладке, к заказу 9,36 м²; пом. 6, 11; л. 49–52
4	Керамогранит 600×1200 мм A8UZ	A8UZ			шт	86	10	коробка	98 шт		19 целых + 67 с подрезкой; 45,03 м² по раскладке, к заказу 70,56 м²; пом. 4, 6, 11; л. 49–52
Сухие смеси и гидроизоляция											
5	Клей плиточный цементный класса C2 TE S1 (ГОСТ Р 56387-2018)	Ceresit CM 17 или аналог			кг	364,55	10	мешок 25 кг	17 меш.	25	слой 5 мм, 1,50 кг/м² на 1 мм; л. 49
6	Затирка цементная класса CG2WA, цвет — по колерной карте	Mapei Ultracolor Plus 132 или аналог			кг	3,61	10	упак. 2 кг	2 упак.	2	расход (a+b)/ab × шов × t × 1,6 кг/м²; л. 49
7	Гидроизоляция обмазочная полимерная, 2 слоя, лента в углах, манжеты на выводах	по выбору подрядчика			м²	17,01	10	ведро по ТУ	по ТУ		пом. 6, 11; расход кг/м² — по ТУ; л. 49
8	Лента демпферная по периметру пола из плитки	по выбору подрядчика			м	24,68	10	рулон	28,00 м		л. 49
9	Смесь цементно-песчаная для стяжки М200 (50 мм, 49 мм, 47 мм, 33 мм)	по выбору подрядчика			м³	4,95	5	мешок по ТУ	по ТУ		S 101,85 м² × толщина; армирование и маяки — по ТУ; л. 53
10	Смесь штукатурная гипсовая для машинного и ручного нанесения по маякам, слой до 10 мм	по выбору подрядчика			м²	291,08	10	мешок по ТУ	по ТУ		пом. 1, 2, 3, 4, 5, 6, 7, 8, 9, 10, 11; расход кг/м² на 1 мм слоя — по ТУ смеси, толщина — по замеру кривизны стен; л. 14, 54–56
Короба из ГКЛВ											
11	Лист ГКЛВ 12,5 мм, 2500 × 1200 мм, обшивка коробов в 2 слоя	по выбору подрядчика			м²	6,46	10	лист 3,00 м²	3,00 лист		инсталляция пом. 6: 1,76 м²; инсталляция пом. 11: 1,47 м²; площадь × 2 слоя; короб К1 над полом — в спецификации ВК; л. 33, 49–52
12	Профиль стальной оцинкованный 27 × 28 мм: каркас коробов (стойки и направляющие)	по выбору подрядчика			м	15,60	10	хлыст 3 м	6 шт		стойки через 400 мм по свободному периметру + направляющие по полу и потолку; крепёж, лента, шпаклёвка швов — по узлу короба; л. 33, 49–52
Слаботочные сети											
13	Кабель домофона — тип по системе поставщика	по выбору подрядчика			м	4,30		бухта по ТУ	5,00 м		по лучам от ЩС**, 1 точ., запас 10 % уже в длине; 2 точ. — предложение листа слаботочки (знак «*» на плане); л. 30
14	Кабель коаксиальный RG-6 (75 Ом) к розеткам ТВ	по выбору подрядчика			м	16,10		бухта по ТУ	17,00 м		по лучам от ЩС**, 1 точ., запас 10 % уже в длине; 2 точ. — предложение листа слаботочки (знак «*» на плане); л. 30
15	Кабель U/UTP кат. 6 (LAN, Wi-Fi и камеры по PoE)	по выбору подрядчика			м	70,30		бухта по ТУ	71,00 м		по лучам от ЩС**, 5 точ., запас 10 % уже в длине; 2 точ. — предложение листа слаботочки (знак «*» на плане); л. 30
16	Гофротруба Ø20 для слаботочных линий, отдельно от силовых	по выбору подрядчика			м	81,60		бухта по ТУ	82,00 м		по длине лучей без участков в канале плинтуса (≈ 90 %); л. 30
17	Розетка компьютерная RJ45, кат. 6, с рамкой и подрозетником	по выбору подрядчика			шт	4		шт	4 шт		LAN1, LAN3, LAN4, LAN5**; серия механизмов — как у розеток и выключателей; л. 26, 27, 30

Допущения и предложения на листе

Основа листа: размеры сняты со скана обмерного плана KV design (см): часть подписей не читается, помещения выровнены по читаемым размерам; контрольный обмер не выполнен (К-1); высота потолка 2650 мм принята по отметкам обмера (H = 2,50…2,66 м, ригель 2,28 м) — уточнить при обмере (К-2); толщины стен 300 / 120 мм приняты, межквартирная стена и колонны — по скану, не замерены (К-1); разрешённая мощность 15 кВт принята по типовым ТУ; при объединении двух квартир — переоформление ТУ (К-4); подрайон климата не задан — принят не северный (жилые от 2,5 м) (К-8).

Знак «**» — предложение проектировщика, заказчиком не утверждено (согласовать с заказчиком): LAN5 — стол Б2 стоит посреди помещения — питание из лючка в полу под столом: трасса в конструкции пола (толщина стяжки — по обмеру) — согласовать с заказчиком; ЩС — щит слаботочный: место и состав; плинтус пом. 1–5, 7–10, акцент пом. 3, фартук пом. 5 — артикул изделия не выбран: позиция описана характеристиками («аналог по характеристикам»), артикул выбирается при закупке; пол пом. 6, 11 — пирог пола: стяжка 33 мм и обмазочная гидроизоляция добавлены разработчиком проекта; артикул изделия не выбран: позиция описана характеристиками («аналог по характеристикам»), артикул выбирается при закупке.

См. лист открытых вопросов (лист 6, записи К-1, К-2, К-4, К-8).

Изм.	Кол.уч	Лист	№ док.	Подп.	Дата
Разраб.		Кырлан А.С.			04.11.26
Пров.					
ГИП					
Н. контр.					
Утв.					

ГД-2026-009-АИ

Квартира 103 м²

Общая площадь 100,72* м² · * размеры со скана, не замерены (реестр — л. 6, 7, К-1)

Дизайн-проект интерьера

Стадия	Лист	Листов
РП	117	120

Спецификация материалов

М б/м

Кырлан Александр Сергеевич

Спецификация материалов (окончание)

Отделочные материалы: чистое количество, запас, упаковка, к заказу · ГОСТ 21.110-2013

Спецификация материалов (ГОСТ 21.110-2013, форма 1) (продолжение)

Поз.	Наименование и техническая характеристика	Тип, марка, артикул	Код продукции	Поставщик	Ед. изм.	Количество				Масса ед., кг	Примечание
						чистое	запас, %	упаковка	к заказу		
18	Розетка телевизионная (коаксиальная) с рамкой и подрозетником	по выбору подрядчика			шт	1		шт	1 шт		ТВ1; серия механизмов — как у розеток и выключателей; л. 26, 27, 30
19	Трубка или монитор домофона (поставка домофонной организации)	по выбору подрядчика			шт	1		шт	1 шт		ДФ1; серия механизмов — как у розеток и выключателей; л. 26, 27, 30
20	Щит слаботочный ЩС**: корпус, DIN-рейка, розетки 220 В	по выбору подрядчика			шт	1		шт	1 шт		ЩС**; серия механизмов — как у розеток и выключателей; л. 26, 27, 30
21	Патч-панель, портов не менее 5	по выбору подрядчика			шт	1		шт	1 шт		серия механизмов — как у розеток и выключателей; л. 26, 27, 30
Лакокрасочные материалы											
22	Краска интерьерная акриловая, матовая, класс истирания 1	Farrow & Ball Modern Emulsion No. 289 «Inchyra Blue — тёмный сине-серый»			л	8,54	10	банка 2,5 л	4 банк		35,60 м² × 2 сл. × 0,12 л/м²; пом. 1, 8, 10; л. 54–56
23	Краска интерьерная акриловая, матовая, класс истирания 1	Farrow & Ball Modern Emulsion No. 291 «School House White — тёплый меловой белый»			л	49,98	10	банка 2,5 л	22 банк		208,26 м² × 2 сл. × 0,12 л/м²; пом. 1, 3, 3 (пот.), 4, 5, 5 (пот.), 8, 9, 10; л. 54–56
24	Краска интерьерная акриловая, глубокоматовая, класс истирания 2	Tikkurila Anti-Reflex 2 S 0502-Y «Белый с лёгкой желтизной»			л	16,28	10	банка 2,7 л	7 банк		67,84 м² × 2 сл. × 0,12 л/м²; пом. 1 (пот.), 2 (пот.), 4 (пот.), 7 (пот.), 8 (пот.), 9 (пот.), 10 (пот.); л. 54–56
25	Краска интерьерная акриловая, матовая, класс истирания 1	Tikkurila Harmony S 0502-Y «Белый с лёгкой желтизной»			л	7,08	10	банка 2,7 л	3 банк		29,50 м² × 2 сл. × 0,12 л/м²; пом. 2, 7; л. 54–56
26	Краска интерьерная акриловая, матовая, класс истирания 1	Farrow & Ball Modern Emulsion No. 255 «Tanner's Brown — тёмный шоколад»			л	4,23	10	банка 2,5 л	2 банк		11,74 м² × 3 сл. × 0,12 л/м²; пом. 3; л. 54–56
27	Краска интерьерная акриловая, матовая, класс истирания 1	Tikkurila Luja 7 S 0502-Y «Белый с лёгкой желтизной»			л	1,45	10	банка 2,7 л	1 банк		6,04 м² × 2 сл. × 0,12 л/м²; пом. 6 (пот.), 11 (пот.); л. 54–56
28	Шпаклёвка финишная полимерная под окраску (стены и потолки, Q3)	по выбору подрядчика			м²	358,98	10	ведро по ТУ	по ТУ		расход кг/м² на слой — по ТУ; л. 54–56
29	Грунтовка акриловая глубокого проникновения, 2 слоя	по выбору подрядчика			м²	391,80	10	канистра по ТУ	по ТУ		расход л/м² — по ТУ; л. 54–56
Погонажные изделия и потолки											
30	Плинтус напольный МДФ под покраску, h=83 мм, крепление к стене	Ultrawood Base 5340, ЛДФ под окраску, 83×15 мм, 2440 мм (арт. LDF-BASE-5340)			м.п.	103,48	10	хлыст 2,4 м	48 шт		пом. 1, 2, 3, 4, 5, 7, 8, 9, 10; длина хлыста — по артикулу; л. 54–56
31	Потолок подвесной ГКЛ/ГКЛВ по каркасу Knauf П113: листы, профили, подвесы, лента, шпаклёвка швов	Knauf П113			м²	96,28		комплект	по л. потолков		площадь — по ведомости потолков; число листов, профилей и подвесов — по шагам каркаса на листе потолков; л. 45–48

Примечания

1. Чистое количество — из ведомости объёмов работ и раскладки плитки; запас — отдельной графой (доска — по ведомости отделки, плитка, краска и плинтус — 10 %); «к заказу» — с запасом и кратно упаковке.
2. Плитка — штуками по раскладке, запас на каждую поверхность. Калибр (рабочий размер) и тон — одной партией на помещение, калибр указать при заказе и сверить с раскладкой до укладки.
3. Краска — 0,12 л/м² на слой (середина вилки 0,10–0,15 л/м²) по фактической площади окраски из ведомости отделки; колеровка одной партией.
4. «По ТУ» — расход задаёт производитель выбранного продукта; количество к заказу — после выбора марки.
5. Штукатурная смесь — на ту же площадь, что строка ВОР «Штукатурка стен» (291,08 м²): площадь одна, расход смеси задаёт производитель.
6. Коробы инсталляции и стояков: ГКЛВ в 2 слоя и профиль 27 × 28 мм считаются по свободным граням коробов (источник — раскладка плиточника и шахты в данных); короб К1 над полом — в спецификации ВК.
7. Потолки ГКЛ: в этой спецификации — площадь системы П113; число листов, профилей и подвесов — по шагам каркаса на листе потолков (подвесы через 1000, несущие через 500, основные через 1200 мм), схема каркаса не выпущена. Сантехника, светильники и мебель — по своим спецификациям.

Допущения и предложения на листе

Основа листа: размеры сняты со скана обмерного плана KV design (см): часть подписей не читается, помещения выровнены по читаемым размерам; контрольный обмер не выполнен (К-1); высота потолка 2650 мм принята по отметкам обмера (Н = 2,50…2,66 м, ригель 2,28 м) — уточнить при обмере (К-2); толщины стен 300 / 120 мм приняты, межквартирная стена и колонны — по скану, не замерены (К-1); разрешённая мощность 15 кВт принята по типовым ТУ; при объединении двух квартир — переоформление ТУ (К-4); подрайон климата не задан — принят не северный (жилые от 2,5 м) (К-8).

Знак «**» — предложение проектировщика, заказчиком не утверждено (согласовать с заказчиком): ЩС — щит слаботочный: место и состав; плинтус пом. 1–5, 7–10, акцент пом. 3, фартук пом. 5 — артикул изделия не выбран: позиция описана характеристиками («аналог по характеристикам»), артикул выбирается при закупке; пол пом. 6, 11 — пирог пола: стяжка 33 мм и обмазочная гидроизоляция добавлены разработчиком проекта; артикул изделия не выбран: позиция описана характеристиками («аналог по характеристикам»), артикул выбирается при закупке.

См. лист открытых вопросов (лист 6, записи К-1, К-2, К-4, К-8).

Изм.	Кол.уч	Лист	№ док.	Подп.	Дата
Разраб.		Кырлан А.С.			04.11.26
Пров.					
ГИП					
Н. контр.					
Утв.					

ГД-2026-009-АИ

Квартира 103 м²

Общая площадь 100,72* м² · * размеры со скана, не замерены (реестр — л. 6, 7, К-1)

Дизайн-проект интерьера	Стадия	Лист	Листов
	РП	118	120
Спецификация материалов (окончание) М б/м	**Кырлан Александр Сергеевич**		

Смета ориентировочная

ПРЕДВАРИТЕЛЬНО · не для производства работ · открыто пунктов: 8 (реестр — л. 6, 7)

Работы, материалы, оборудование, услуги и резерв · цены — ориентир по открытым прайсам, не коммерческое предложение

Сводная смета (цены на 21.09.2026, Москва)

№	Наименование работ, материалов, услуг	Ед. изм.	Кол-во	Цена за ед., ₽	Стоимость, ₽			Чей подряд	Срок поставки, дн.	Основание	Источник цены
					план	факт	разница				
Работы — по ведомости объёмов работ											
1	Демонтаж и черновые работы (без 5 поз. по КП)	раздел	1		364 151			бригада		ВОР, поз. 1–10; л. 114–116	по ВОР
2	Инженерные системы (без 12 поз. по КП)	раздел	1		190 135			бригада		ВОР, поз. 11–33; л. 114–116	по ВОР
3	Чистовые работы (без 1 поз. по КП)	раздел	1		809 479			бригада, поставщик		ВОР, поз. 34–50; л. 114–116	по ВОР
Материалы — по спецификации материалов											
4	Инженерная доска	м²	88,30	4 513	398 498			поставщик		спецификация, поз. 1	Ц7
5	Керамогранит 600×600 мм	м²	9,36	1 800	16 848			поставщик		спецификация, поз. 3	Ц6
6	Керамогранит 600×1200 мм	м²	70,56	3 500	246 960			поставщик		спецификация, поз. 4	Ц6
7	Клей плиточный цементный класса C2 TE S1	меш.	17	1 800	30 600			поставщик		спецификация, поз. 5	Ц7
8	Затирка цементная класса CG2WA	упак.	2	1 000	2 000			поставщик		спецификация, поз. 6	Ц7
9	Краска Farrow & Ball Modern Emulsion, банка 2,5 л	банк	28	5 800	162 400			поставщик		спецификация, поз. 22, 23, 26	Ц7
10	Краска Tikkurila (Anti-Reflex 2, Harmony, Luja 7), банка 2,7 л	банк	11	3 510	38 610			поставщик		спецификация, поз. 24, 25, 27	Ц6
11	Плинтус напольный МДФ под покраску	шт	48	368	17 664			поставщик		спецификация, поз. 30	Ц7
12	Прочие материалы с расходом по ТУ (клей для доски, гидроизоляция, демпферная лента, смесь для стяжки, смесь штукатурная гипсовая для машинного и ручного нанесения по маякам, лист гклв 12, профиль стальной оцинкованный 27 × 28 мм: каркас коробов (стойки и направляющие), кабель слаботочки, гофра слаботочки, изделия слаботочки, шпаклёвка, грунтовка, каркас и ГКЛ потолков)	компл	1	по КП				поставщик		спецификация, поз. 2, 7, 8, 9, 10, 11, 12, 13, 14, 15, 16, 17, 18, 19, 20, 21, 28, 29, 31	
Оборудование и мебель — поставка по спецификациям											
13	Кухонный гарнитур по проекту кухни, изготовление и монтаж (4–8 нед.)	компл	1	по КП				поставщик	не задан; ориентир 4–8 нед. от замера	л. 72–75	

Допущения и предложения на листе

Основа листа: размеры сняты со скана обмерного плана KV design (см): часть подписей не читается, помещения выровнены по читаемым размерам; контрольный обмер не выполнен (К-1); высота потолка 2650 мм принята по отметкам обмера (Н = 2,50…2,66 м, ригель 2,28 м) — уточнить при обмере (К-2); толщины стен 300 / 120 мм приняты, межквартирная стена и колонны — по скану, не замерены (К-1); разрешённая мощность 15 кВт принята по типовым ТУ; при объединении двух квартир — переоформление ТУ (К-4); подрайон климата не задан — принят не северный (жилые от 2,5 м) (К-8).

См. лист открытых вопросов (лист 6, записи К-1, К-2, К-4, К-8).

Изм.	Кол.уч	Лист	№ док.	Подп.	Дата
Разраб.		Кырлан А.С.			04.11.26
Пров.					
ГИП					
Н. контр.					
Утв.					

ГД-2026-009-АИ

Квартира 103 м²

Общая площадь 100,72* м² · * размеры со скана, не замерены (реестр — л. 6, 7, К-1)

Дизайн-проект интерьера

Стадия	Лист	Листов
РП	119	120

Смета ориентировочная

М б/м

Кырлан Александр Сергеевич

Смета ориентировочная (окончание)

ПРЕДВАРИТЕЛЬНО · не для производства работ · открыто пунктов: 8 (реестр — л. 6, 7)

Работы, материалы, оборудование, услуги и резерв · цены — ориентир по открытым прайсам, не коммерческое предложение

Сводная смета (цены на 21.09.2026, Москва) (продолжение)

№	Наименование работ, материалов, услуг	Ед. изм.	Кол-во	Цена за ед., ₽	Стоимость, ₽			Чей подряд	Срок поставки, дн.	Основание	Источник цены
					план	факт	разница				
14	Двери скрытого монтажа с коробом под покраску, поставка	шт	8	по КП				поставщик	не задан; ориентир ≈ 30 дн.	л. 16, 17	
15	Оборудование заказчика слаботочных сетей: точка доступа wi-fi — 1 шт; коммутатор — 1 шт	компл	1	по КП				заказчик		л. 26, 27	
16	Сантехника, светильники, мебель и предметы интерьера	компл	1	по КП				поставщик		л. 42; л. 43, 44; л. 77; л. 20–22	
Прочие работы и услуги											
17	Вынос и вывоз строительного мусора	м³		по факту				бригада		после демонтажа	
18	Подъём материалов на этаж (лифтом или вручную — по договору)	т		по факту				бригада		по массе поставки	
19	Доставка чистовых материалов, 10 % от поставки			10 %	91 358			поставщик		от суммы материалов	
20	Уборка после ремонта	м²	100,72	по факту				бригада		S квартиры	
	Итого работы				**1 363 765**						
	Итого материалы				**913 580**						
	Итого прочие услуги				**91 358**						
	Резерв на непредвиденные работы и материалы, 15 %				**355 305**						
	ВСЕГО ориентировочно (без оборудования и позиций по КП)				**2 724 008**						

Примечания

1. Смета ориентировочная, не коммерческое предложение: объёмы — из ведомости объёмов работ и спецификации материалов, цены — нижняя граница открытых прайсов Москвы (цены на 21.09.2026); перед договором цены подтвердить у подрядчика и поставщиков.
2. Источники цен: Ц1 — Домашний мастерок: прайс на отделочные работы, 2026; Ц2 — Домашний мастерок: прайс на плиточные работы, 2026; Ц3 Домашний мастерок: прайс на электромонтажные работы, 2026; Ц4 — Профи ремонтник: штукатурно-малярные работы; Ц5 — Profi.ru: укладка керамогранита на стены, Москва 2026; Ц6 — knowledge/spec-materials.md, разд. 1 и 3: ориентир по сегментам; Ц7 — Розница Москвы, 09.2026: Лемана ПРО, KGSnab, официальный дилер Farrow & Ball.
3. В итог не вошли позиции «по КП» и «по факту»: оборудование и мебель, двери, материалы с расходом по ТУ, вывоз мусора, подъём и уборка.
4. Доставка — 10 % от материалов, резерв — 15 % (частный ремонт 10–20 %) отдельными строками, в количествах не спрятаны. Графы «факт» и «разница» заполняются по актам.

Допущения и предложения на листе

Основа листа: размеры сняты со скана обмерного плана KV design (см): часть подписей не читается, помещения выровнены по читаемым размерам; контрольный обмер не выполнен (К-1); высота потолка 2650 мм принята по отметкам обмера (Н = 2,50…2,66 м, ригель 2,28 м) — уточнить при обмере (К-2); толщины стен 300 / 120 мм приняты, межквартирная стена и колонны — по скану, не замерены (К-1); разрешённая мощность 15 кВт принята по типовым ТУ; при объединении двух квартир — переоформление ТУ (К-4); подрайон климата не задан — принят не северный (жилые от 2,5 м) (К-8).
См. лист открытых вопросов (лист 6, записи К-1, К-2, К-4, К-8).

Изм.	Кол.уч	Лист	№ док.	Подп.	Дата
Разраб.		Кырлан А.С.			04.11.26
Пров.					
ГИП					
Н. контр.					
Утв.					

ГД-2026-009-АИ

Квартира 103 м²

Общая площадь 100,72* м² · * размеры со скана, не замерены (реестр — л. 6, 7, К-1)

Дизайн-проект интерьера

Стадия	Лист	Листов
РП	120	120

Смета ориентировочная (окончание)

М б/м

Кырлан Александр Сергеевич