L

LINEA

ДИЗАЙН-ПРОЕКТ ИНТЕРЬЕРА

Квартира 55 м²

кухня-гостиная и спальня

ПАЛИТРА ОТДЕЛКИ

NCS S 1502-Y50	NCS S 1002-Y50	V503
44 %	32 %	24 %

АВТОР ПРОЕКТА

Кырлан Александр Сергеевич

Ноябрь 2026



План расстановки мебели · М 1:50

ОБЩАЯ ПЛОЩАДЬ	ПОМЕЩЕНИЙ	СТАДИЯ	ШИФР	ОСНОВА
55,23 м²	6, из них жилых 2	Проект · предварительно	ГД-2026-006-АИ	план заказчика, без обмера

Как оставить правку: кнопка «Правка к этому листу» в правом верхнем углу любого листа · все листы проекта: дизайн-студия-квартир.рф/review.html?p=gost-kv58

выпуск 04.11.2026 № e0dc2f2b59 · стр. 1 из 71

Объект

Квартира 58 м²: 57,6 м², помещений 6, из них жилых 2.

Стиль: скандинавский 100 %. Стадия: предварительный альбом без обмера, планировка по плану заказчика.

Открытых вопросов 7, конфликтов разделов 0; изменений утверждено 0, ждут подписи 3.

Розетки и выводы

19 розеток (рамок 17), 3 вывода кабеля под технику и свет, 6 групп щита — всё с высотами от чистого пола: листы 31, 32.

Что решено (подписано вами)

Подписанных решений пока нет.

Что ждёт вашего ответа

К-1 — Вентканалы на плане заказчика не показаны: ВК-1 принят у перегородки ванной и санузла (со стороны прихожей), ВК-2 — у кухни.

К-2 — Ванная (пом. 3), 2140 × 1380 мм в чистоте, проём Д-4 у стены Б.

К-3 — Скрытые двери Д-2, Д-3, Д-4 стоят в существующих проёмах прихожей, размеров в свету нет: короб скрытой двери шире и выше полотна на 100–120 / 50–80 мм, полотно по проёму 2100…

К-4 — Климатический подрайон (СП 131.13330) не задан: принят не северный — жилые комнаты и кухня под потолком от 2,5 м (СП 54, п. 5.12).

К-5 — Основа альбома — план заказчика без контрольного обмера: размеры помещений сняты с плана, высота потолка 2700 мм и толщины стен (наружные 250 мм, перегородки 120 мм) приняты —…

К-6 — Разрешённая мощность 15 кВт принята по типовой квартире, технических условий в материалах объекта нет.

К-7 — Места стиральной машины в квартире не было.

Предложено, ждёт подписи

ИЗ-1 — ТВ1 (2400), LAN1 (2550) и розетка приставки (2400, H=300) — на стене Г по оси тумбы ОБ_01.

ИЗ-2 — Диван M_08 привязка 1000…3200 — перед проёмом 800 мм.

ИЗ-3 — КВ-1 — стена Г, привязка 300…1200 (простенок у окна 1), КН-1 — стена А, простенок между окнами 2400…3200.

выпуск 04.11.2026 № e0dc2f2b59 · стр. 2 из 71

					Проект: Квартира 58 м²		
	Лист	№ док.	Подпись	Дата	Ваш проект на одной странице	Стадия	Лист	Листов
Дизайнер	Кырлан А.С.			04.11.26		П	2	71

Список листов

Лист	Наименование
1	Титульный лист
2	Ваш проект на одной странице
3	Список листов
4	Как читать альбом
5	План планировки от заказчика
6	План монтажный
7	Кухня (пом. 1). Монтажная схема
8	Шкафы. Монтажная схема
9	Карта покрытий стен
10	Колерная карта
11	План размещения мебели и оборудования
12	Спецификация мебели и оборудования
13	Ведомости изделий, техники и фурнитуры
14	План выводов сантехники
15	Схема разводки водопровода и канализации
16	Аксонометрическая схема В1 (холодное водоснабжение)
17	Аксонометрическая схема Т3 (горячее водоснабжение)
18	Аксонометрическая схема К1 (канализация)
19	Развёртки мокрых зон: выводы ВК. Кухня-гостиная
20	Развёртки мокрых зон: выводы ВК. Ванная (лист 1 из 2)
21	Развёртки мокрых зон: выводы ВК. Ванная (лист 2 из 2)
22	Развёртки мокрых зон: выводы ВК. Санузел
23	Спецификация сантехнического оборудования
24	Раскладка плитки. Ванная. Развёртки стен
25	Раскладка плитки. Санузел. Развёртки стен
26	План размещения дверей
27	Ведомость заполнения проёмов
28	План потолков
29	Разрезы и узлы потолков
30	Разрезы и узлы потолков (продолжение)
31	Однолинейная схема щита
32	План розеток и электровыводов
33	План слаботочных сетей
34	План освещения
35	Техническое задание на подбор светильников
36	Управление светильниками
37	План вентиляции
38	План отопления
39	План покрытий пола
40	Раскладка плитки. Планы полов
41	Раскладка плитки. Прихожая
42	Развёртка стены В. Кухня-гостиная (пом. 1), кухонный фронт
43	Привязки электроточек и выводов ВК, стена В. Кухня-гостиная (пом. 1)
44	Развёртка стены А. Кухня-гостиная (пом. 1)
45	Развёртка стены Б. Кухня-гостиная (пом. 1)
46	Развёртка стены Г. Кухня-гостиная (пом. 1)
47	Развёртка стены А. Спальня (пом. 2)
48	Развёртка стены Б. Спальня (пом. 2)
49	Привязки электроточек, стена Б. Спальня (пом. 2)
50	Развёртка стены В. Спальня (пом. 2)
51	Развёртки стен А, Б. Ванная (пом. 3)
52	Развёртки стен В, Г. Ванная (пом. 3)
53	Привязки электроточек и выводов ВК, стена В. Ванная (пом. 3)
54	Развёртки стен А, Б. Санузел (пом. 4)
55	Развёртки стен В, Г. Санузел (пом. 4)
56	Развёртка стены А. Прихожая (пом. 5)
57	Развёртки стен Б, Г. Прихожая (пом. 5)
58	Развёртка стены В. Прихожая (пом. 5)
59	Привязки электроточек, стена В. Прихожая (пом. 5)
60	Развёртки стен А, Б. Гардеробная (пом. 6)
61	Развёртка стены Г. Гардеробная (пом. 6)
62	Открытые вопросы, принятые допущения и конфликты. Лист 1 из 2
63	Открытые вопросы, принятые допущения и конфликты. Лист 2 из 2
Д_1	Шкаф-купе М_15
Д_2	Система хранения М_16
Д_3	Кухня (пом. 1). Развёртка гарнитура
С1	Ведомость отделки помещений
С2	Спецификация отделочных материалов
С3	Список покупок
С4	Список покупок (окончание)
С5	Узлы

Общие указания

1. Размеры даны в мм от чистовых поверхностей стен: слой штукатурки 20 мм по блоку и 5 мм шпаклёвки по ГКЛ учтён. Перед заказом встроенной мебели — контрольный обмер после штукатурки.
2. Привязки мебели — от стен и углов помещения, а не от другой мебели.
3. Розетки, выводы и выключатели под мебель — см. лист 32 «План розеток и электровыводов»; сантехприборы и выводы воды — лист 14.
4. План расстановки не является документацией для изготовления мебели: изделия — по чертежам мебельщика; покупную мебель заменять только на изделия не больше габарита из спецификации (лист 12).
5. Встроенная мебель «стена в стену» — с зазором 10 мм с каждой стороны или с компенсаторами.
6. Развёртки — вид на стену изнутри помещения, по часовой стрелке; расположение стен на схеме листа развёртки; размеры — в мм по чистовым поверхностям; отметки — в м от ±0,000; высоты Н — от чистого пола помещения до оси изделия, у декора — до центра.
7. Красная цепочка — привязки электроточек и выводов по осям от угла чистовых стен; высота Н — у знака, от чистого пола до оси; высоты мебели, проёмов и границ отделки колонкой отметок слева. Стена с 5 и более точками или с мелкими звеньями привязок показана двумя видами: архитектурная развёртка (мебель, отделка, проёмы, высоты) и вид «Привязки» на отдельном листе — точки и выводы с марками, одна цепочка по осям и таблица привязок (каждая точка — строка).
8. У знака электроточки: марка (Р — розетка, S — выключатель, Св — светильник, ЭВ вывод кабеля), ×N — число постов в рамке, гр. — группа щита, Н — высота оси от чистого пола, мм; группы по клавишам выключателя — на листе выключателей.
9. Схема мебели, приборов и декора не является технической документацией для производства мебели; габариты — по паспортам изделий.
10. Марки позиций: М_NN — мебель, ОБ_NN — оборудование, С_NN — сантехника; О-N отделка (ведомость отделочных материалов, серия С).
11. Размеры мебели и изделий на заказ уточнить по месту после отделочных работ.

					Проект: Квартира 58 м²
	Лист	№ док.	Подпись	Дата	
Дизайнер	Кырлан А.С.			04.11.26	Список листов
					Стадия: П; Лист: 3; Листов: 71

Что в альбоме

Альбом — дизайн-проект с рабочими чертежами для ремонта. Листы идут в порядке работ: титул и вводные, реестр открытых вопросов и решений, планы (обмер, монтаж стен, мебель, двери, потолки, полы), инженерия (сантехника, электрика, вентиляция и отопление), развёртки стен с визуализациями помещений, чертежи мебели, ведомости материалов и узлы.

Вам как заказчику — титул, эта вводная, «Ваш проект на одной странице», реестр вопросов, план мебели, визуализации и развёртки, ведомости мебели и материалов. Подрядчику — всё остальное: монтажные планы, привязки выводов и розеток, узлы, ведомости объёмов.

Знаки на листах

Без знака — решение утверждено или подтверждено обмером.

Что проверить до ремонта

1. Розетки у кровати и рабочего места: хватает ли их с каждой стороны кровати и над столом (план розеток — лист 32).

2. Выводы под технику — варочная панель, духовка, посудомойка, стиральная машина, бойлер: совпадают ли с выбранными моделями (листы 12, 32).

3. Высоты розеток, выключателей и выводов даны от чистого пола: если мебель или техника будут другими — скажите до штробления стен.

Номера записей

К-N — открытый вопрос: чего не хватает или что выбрать (варианты и рекомендация — в тексте). Пока ответа нет, действует строка «если решения нет».

Кф-N — конфликт между разделами (например, мебель и радиатор в одном месте); закрывается решением, которое записывается как ИЗ-N.

ИЗ-N — изменение проекта: что было, что стало и кто утвердил. Изменение без подписи предложение.


Все записи — на листе реестра сразу после вводных; на других листах на них стоят ссылки.

Почему альбом предварительный

Обмера на объекте не было: размеры взяты с плана заказчика. Технические условия (мощность, вода, вентиляция дома) не получены, часть решений ждёт вашего ответа. Пока в реестре есть открытые вопросы, альбом предварительный — пометка в штампе снимается закрытием вопросов, а не стиранием.

Правку к любому листу можно оставить по кнопке «Правка к листу» или на сайте студии: дизайн-студия-квартир.рф — укажите номер листа и что изменить.

3 круга правок входят в цену; условия — в договоре и на странице вашего заказа на сайте студии.

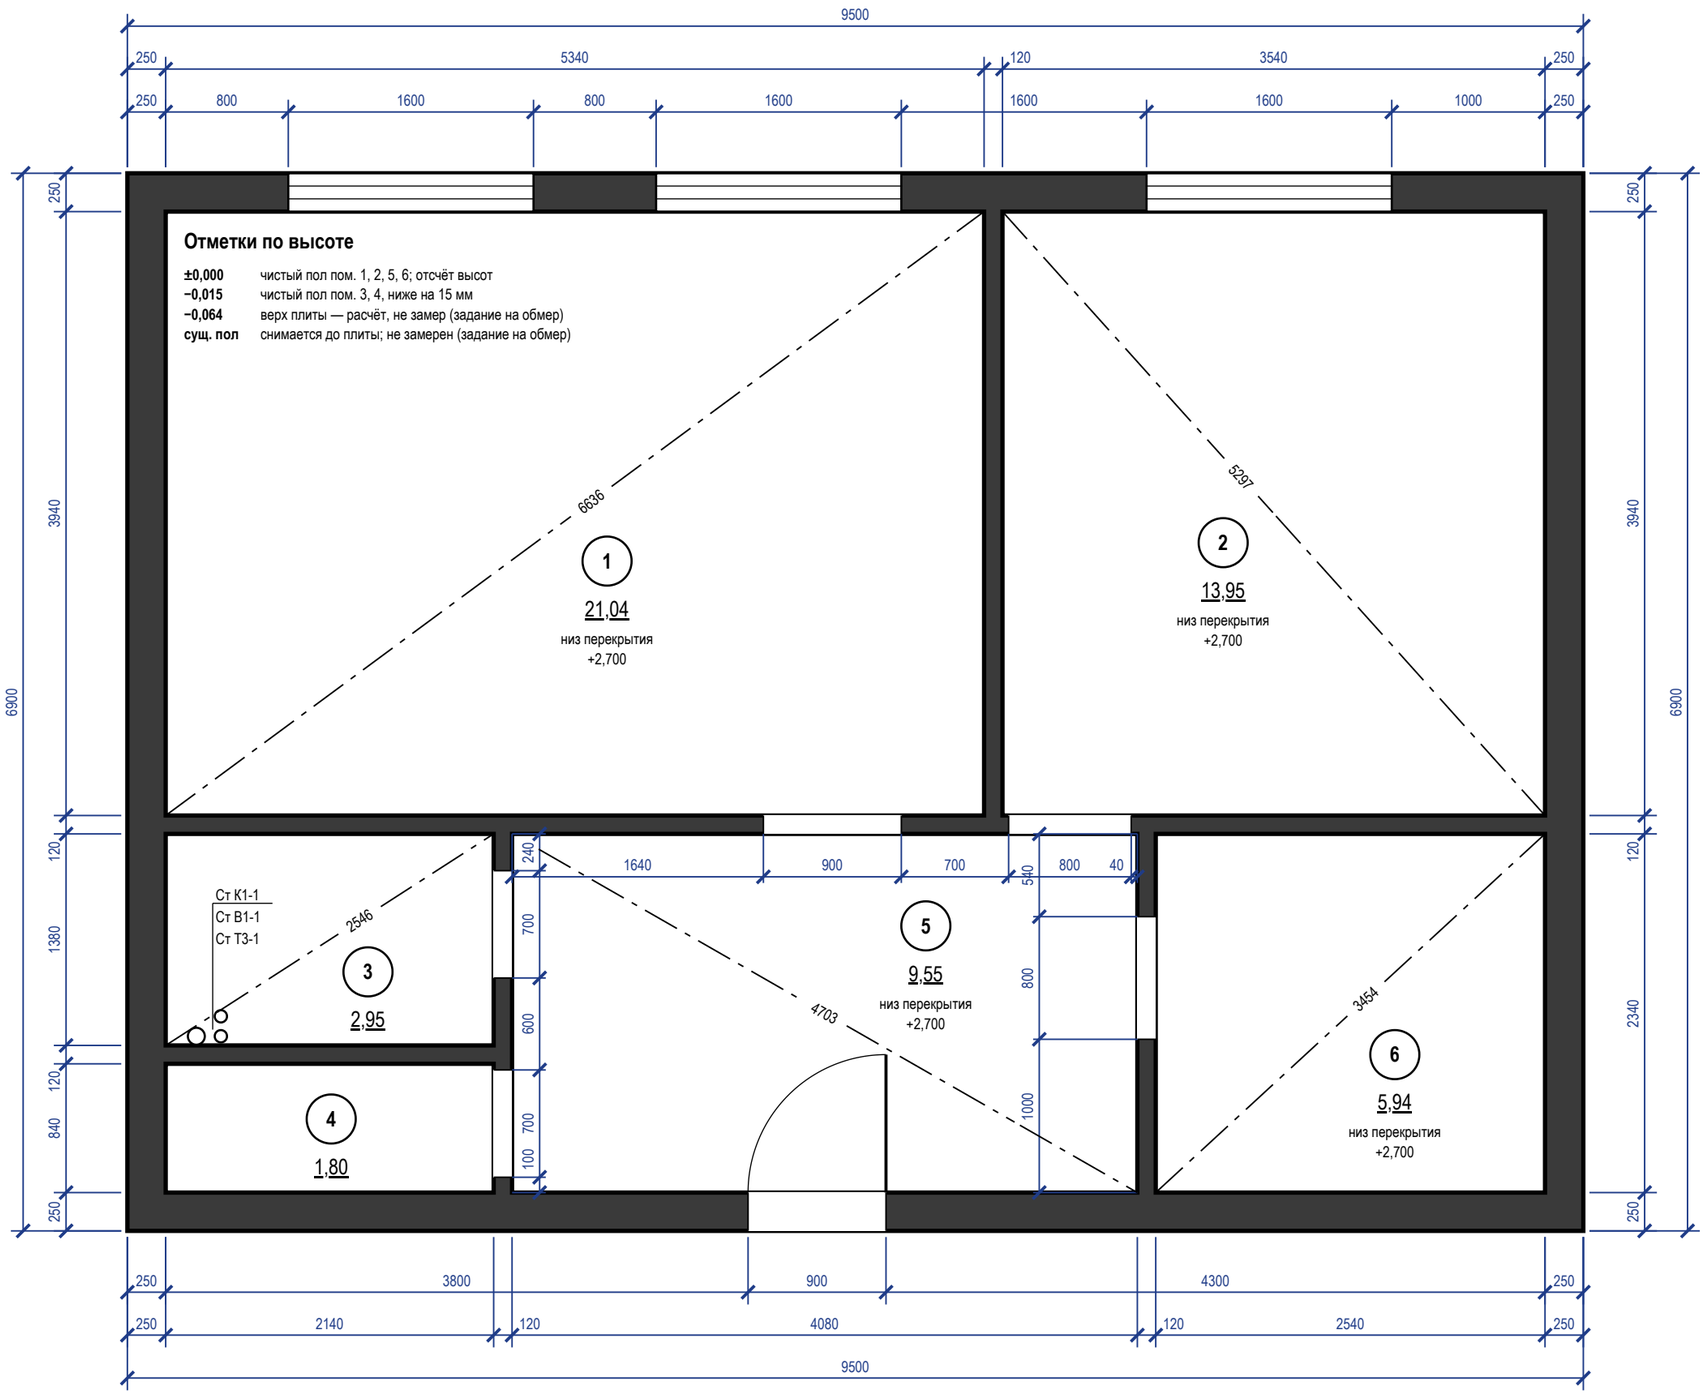

Экспликация помещений

№	Наименование	Площадь, м²
1	Кухня-гостиная	21,04
2	Спальня	13,95
3	Ванная	2,95
4	Санузел	1,80
5	Прихожая	9,55
6	Гардеробная	5,94
	Итого (общая площадь)	**55,23**


Условные обозначения

- существующие стены (сечение)
- окно (рама, остекление)
- проём существующий, без заполнения (откосы)
- стояк: К1 — канализация, В1 — ХВС, Т3 — ГВС
- диагональ помещения — контроль прямоугольности
- (1) номер помещения, площадь м²

Примечания

1. Размеры — в мм по чистым поверхностям стен до отделки (по плану заказчика); площади — в м² по тем же размерам. До начала работ выполнить контрольный обмер.
2. За отметку ±0,000 принят чистый пол, не существующий (блок отметок). «Низ перекрытия» у марки помещения — отметка низа перекрытия от ±0,000, как на развёртках и плане потолков (не высота потолка: потолок — по плану потолков).
3. Толщины стен: наружные 250 мм, перегородки 120 мм; отличающиеся толщины и уступы — размерами на плане.
4. Несущие стены не определены: до технического заключения все стены считать несущими; проёмы и штробы в них не выполнять.
5. Дверные проёмы показаны без заполнения (двери — лист 27); высота дверных проёмов 2100 мм; низ окон (подоконник) 800 мм от чистого пола, высота окон 1600 мм.
6. Диагонали — контрольные размеры; расхождение более 5 мм подписать на плане как перекос.
7. Размеры проверить на месте до начала работ; расхождение контрольных промеров ≤ 2 %.

					Проект: Квартира 58 м²	**М 1:40**
	Лист	№ док.	Подпись	Дата	План планировки от заказчика	Стадия / Лист / Листов
Дизайнер	Кырлан А.С.			04.11.26		П / 5 / 71

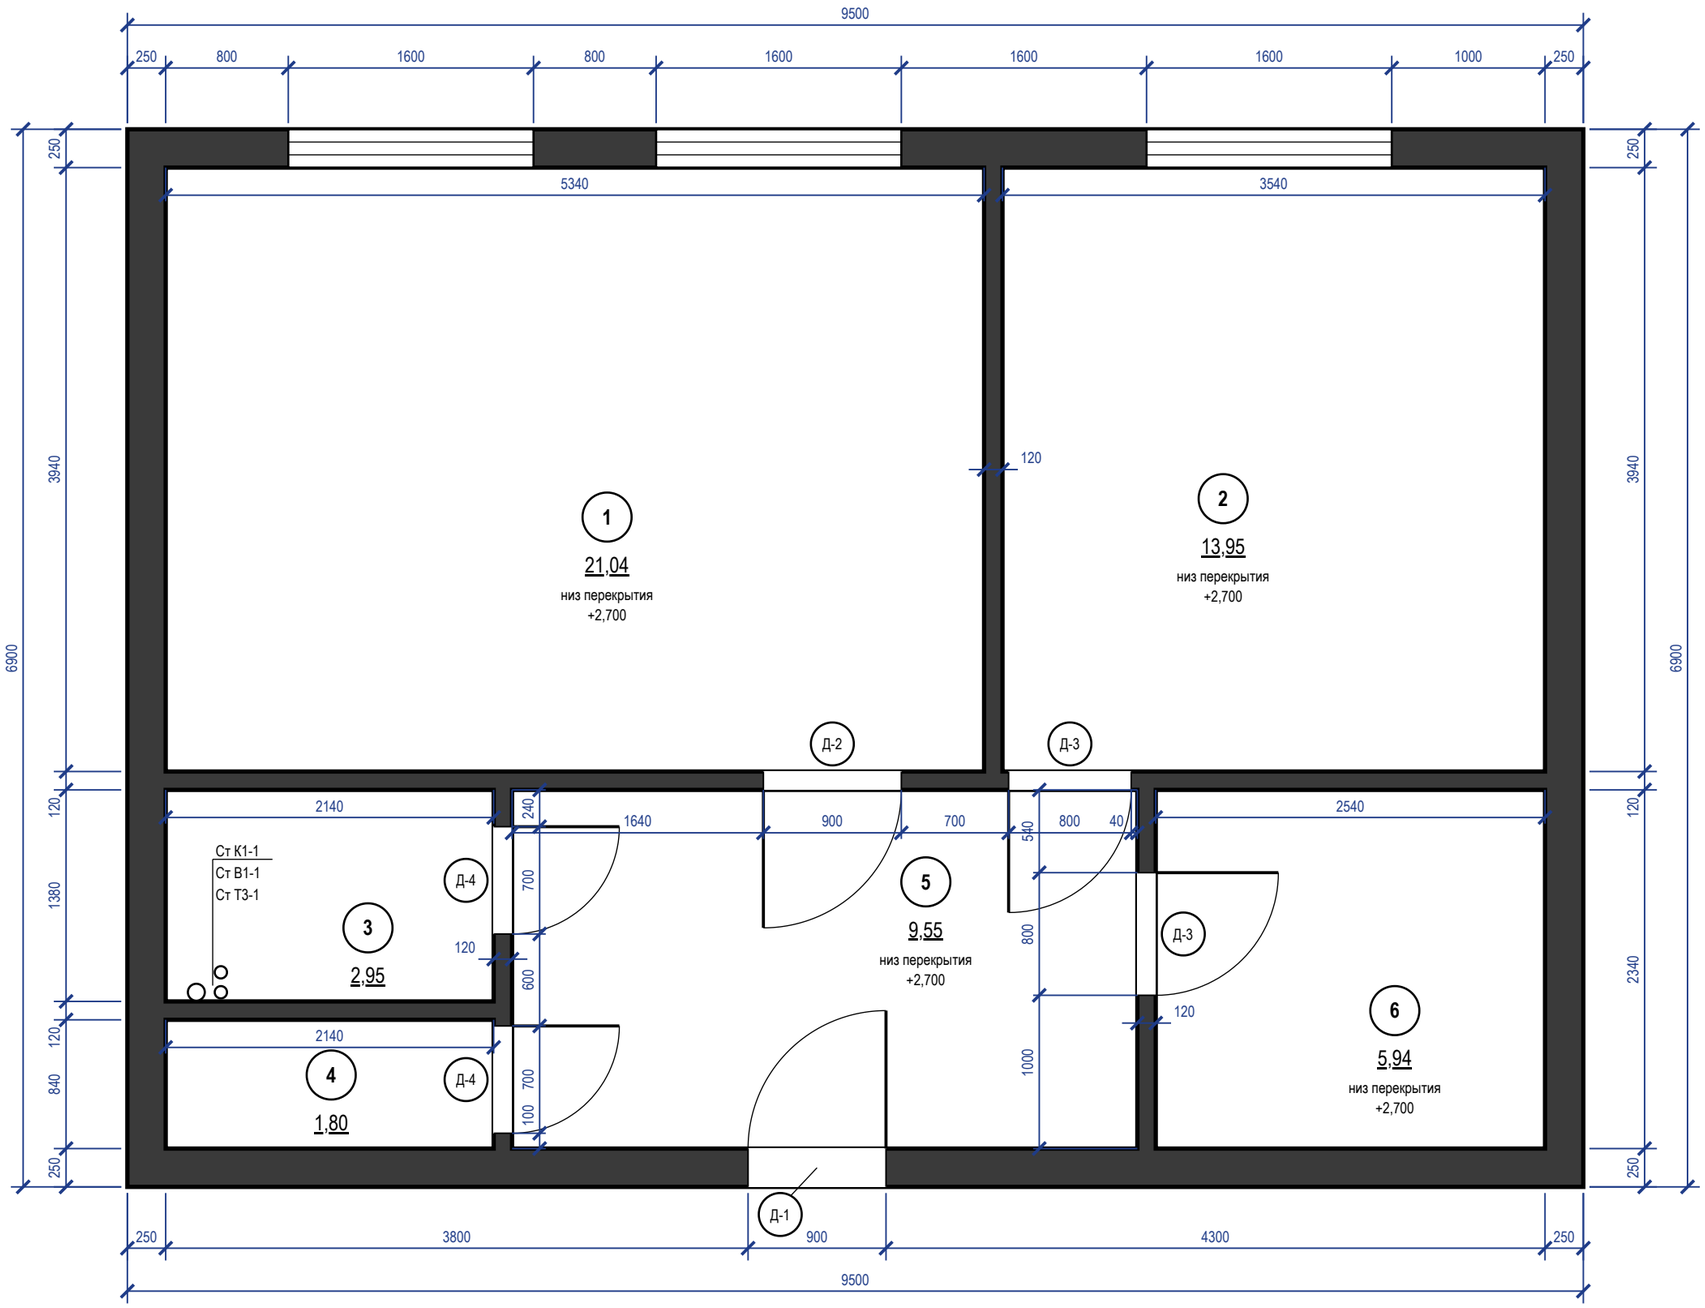

Экспликация помещений

№	Наименование	Площадь, м²
1	Кухня-гостиная	21,04
2	Спальня	13,95
3	Ванная	2,95
4	Санузел	1,80
5	Прихожая	9,55
6	Гардеробная	5,94
	Итого (общая площадь)	**55,23**

Таблица проёмов


Марка	Наименование	Проём ш×в, мм	Полотно (расч.)
Д-1	Дверь входная	900×2100	блок — задать
Д-2	Дверь скрытого монтажа	900×2100	800×2000
Д-3	Дверь скрытого монтажа	800×2100	700×2000
Д-4	Дверь скрытого монтажа	700×2100	600×2000

Примечания


1. Размеры — в мм от чистовых поверхностей стен до отделки; размеры уточнить по месту до начала работ.
2. Д-N, ПР-N в кружке — марка проёма: проём и полотно — по таблице проёмов, «расч.» — полотно по проёму, заказ — по выбранной модели; ведомость, отделка и фурнитура — лист 27.
3. Несущие стены не изменять: проёмы, ниши и штробы в них — только по техническому заключению.
4. «расч.» — полотно, выведенное из проёма по запасу каталогов; заказ — по таблице проёмов выбранной модели; Д-2, Д-3, Д-4: проём 2100, а под полотно 2000 по каталогам нужен 2050–2080, под 2100 — 2150–2180: высоту проёма — по модели; Д-1: входной блок по ГОСТ 31173-2016 — задать при выборе блока.

					Проект: Квартира 58 м² — **М 1:40**
	Лист	№ док.	Подпись	Дата	План монтажный
Дизайнер	Кырлан А.С.			04.11.26	Стадия: П; Лист: 6; Листов: 71

Привязка выводов и крепление модулей

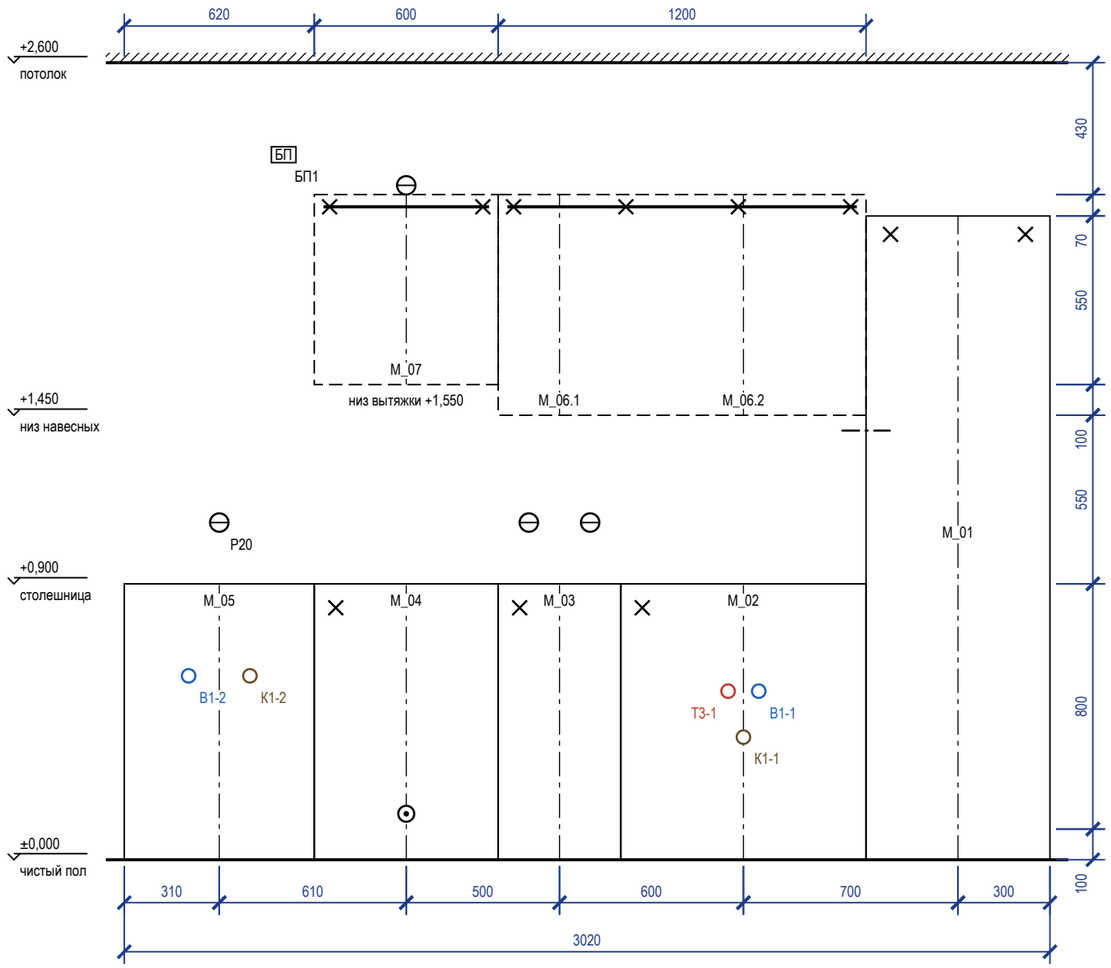

План столешницы

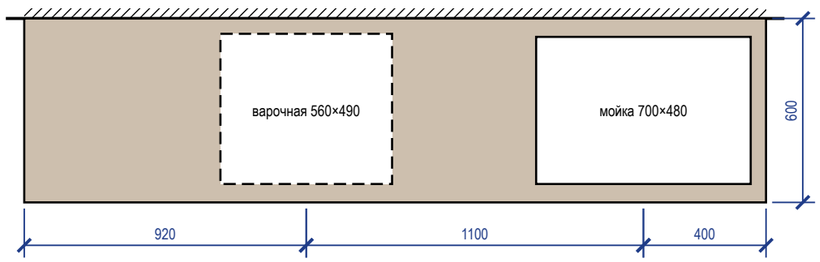

Примечания

1. Выводы — по проекту электрики и ВК; привязка по горизонтали — от оси модуля (плюс — вправо по виду), по высоте — от чистого пола до оси вывода.
2. Пенал — уголки к стене 2 шт. сверху; нижние модули — стяжками между собой и уголком к стене; ряд выставить по уровню опорами цоколя.
3. Розетки над столешницей — не ниже 150 мм над ней и не за корпусом техники; розетка за ПММ, духовым шкафом и холодильником — только в соседнем модуле или в зоне цоколя с доступом.
4. Столешница — вырезы по шаблонам выбранных моделей мойки и варочной панели; торцы у стены — герметик, пристеночный плинтус.

Привязка выводов к осям модулей

Код	Назначение	Модуль	От оси, мм	H, мм	Размещение
B1-2	B1 — кран машины	M_05	−100	600	в нише стиральной машины, за машиной (доступ — выдвинуть машину)
P20	розетка — стиральная машина	M_05	0	1100	над столешницей (фартук)
K1-2	K1 Ø40 — стиральная машина	M_05	+100	600	в нише стиральной машины, за машиной (доступ — выдвинуть машину)
БП1	блок питания	M_05	+210	2300	над столешницей (фартук)
	вывод кабеля — варочная панель	M_04	0	150	в соседнем модуле, за ящиком
	розетка — вытяжка (встроена в дно M_07)	M_07	0	2200	в навесном модуле
	розетка — рабочая зона	M_03	−100	1100	над столешницей (фартук)
	розетка ×2 — рабочая зона	M_03	+100	1100	над столешницей (фартук)
T3-1	T3 — межос. 100	M_02	−50	550	в модуле мойки
K1-1	K1 Ø50 — мойка	M_02	0	400	в модуле мойки
B1-1	B1 — межос. 100	M_02	+50	550	в модуле мойки
	светодиодная лента — подсветка столешницы	M_01	−300	1400	за пеналом

Зазоры под отделку


Поверхность	Отделка	Зазор, мм	Учесть
фартук	плитка / стеновая панель	10	от чернового основания до корпуса навесных и столешницы
стены	окраска	5	под штукатурку и шпаклёвку за пеналом
пол	инженерная доска		цоколь — после укладки пола, опоры ±20 мм

Условные обозначения


- нижний модуль, пенал (контур)
- невидимый контур: навесной модуль, корпус под столешницей
- ось модуля (от неё — привязка вывода)
- анкер / уголок крепления к стене
- розетка на стене
- вывод кабеля к технике
- B1 — вывод воды B1 / T3, канализации K1

					Проект: Квартира 58 м²	M 1:20
	Лист	№ док.	Подпись	Дата		
Дизайнер	Кырлан А.С.			04.11.26	Кухня (пом. 1). Монтажная схема	Стадия: П; Лист: 7; Листов: 71

Шкаф-купе М_15 (пом. 5)

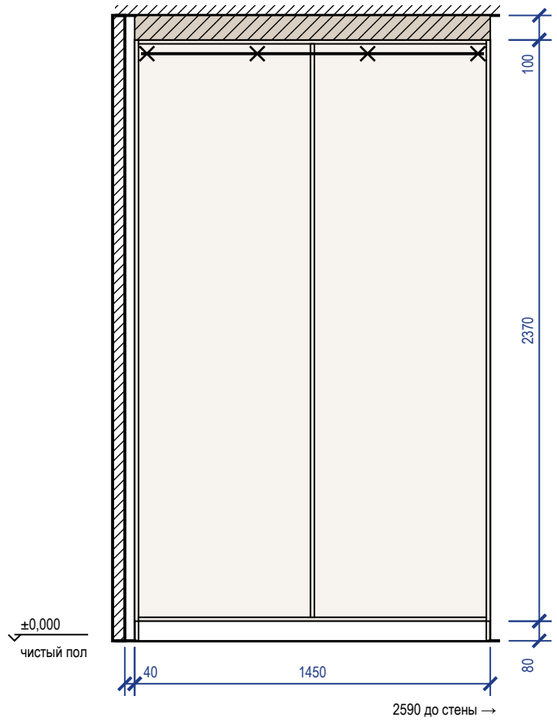

Система хранения М_16 (пом. 6)

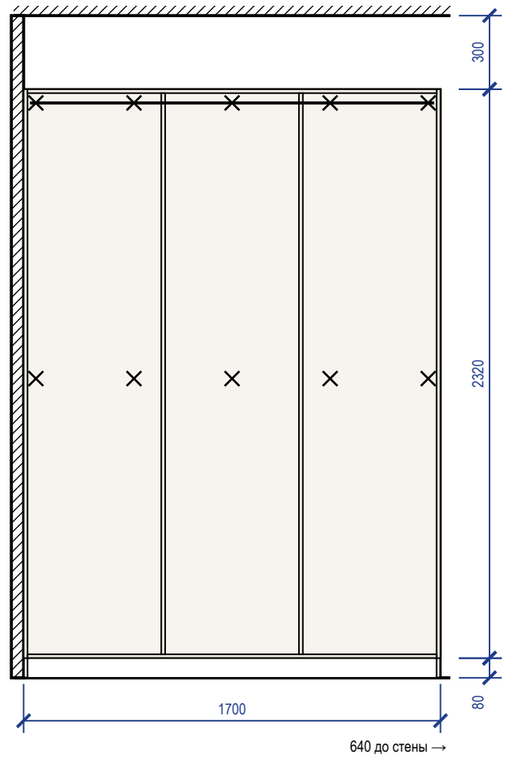

Крепление и зазоры под отделку

Марка	Помещение, стена	Основание	Отделка стены	Зазор, мм	Крепёж по планке	От опрокидывания
М_15	Прихожая (5), стена В	по основанию — см. таблицу крепежа	окраска	5	анкер 4 шт., шаг 450	уголки 2 шт.
М_16	Гардеробная (6), стена Б	по основанию — см. таблицу крепежа	окраска	5	анкер 10 шт. (2 ряда)	крепление к стене, 3 точки

Крепёж по основанию стены

Основание стены	Крепёж
бетон, ж/б	анкер-шуруп 7,5×72 или дюбель 8×60 с шурупом 5×70
кирпич полнотелый	дюбель 8×80 с шурупом 5×90
газобетон, пазогребень	дюбель для газобетона 10×100 или химический анкер
гипсокартон	закладная до обшивки (брус 40×80 или фанера 18 мм), саморез в закладную

Условные обозначения

- × — анкер / уголок крепления к стене
- корпус и полки ЛДСП (вид на стену)
- компенсатор — короб до потолка

Примечания


1. Установочные размеры — от чистого пола и чистых стен; перед установкой контрольный замер после отделки.
2. Порядок: корпус выставить по уровню опорами цоколя → закрепить к стене по задней планке → навесить двери и фасады, отрегулировать зазоры → подогнать и закрепить компенсатор.
3. Анкеры — с шагом не более 500 мм, не ближе 50 мм от края планки; на ГКЛ только в закладную, установленную до обшивки.
4. Скрытые коммуникации под анкеры проверить детектором; трассы электрики по плану розеток.

	Лист	№ док.	Подпись	Дата
Дизайнер	Кырлан А.С.			04.11.26

Проект: Квартира 58 м² — **М 1:25**

Шкафы. Монтажная схема

Стадия	Лист	Листов
П	8	71

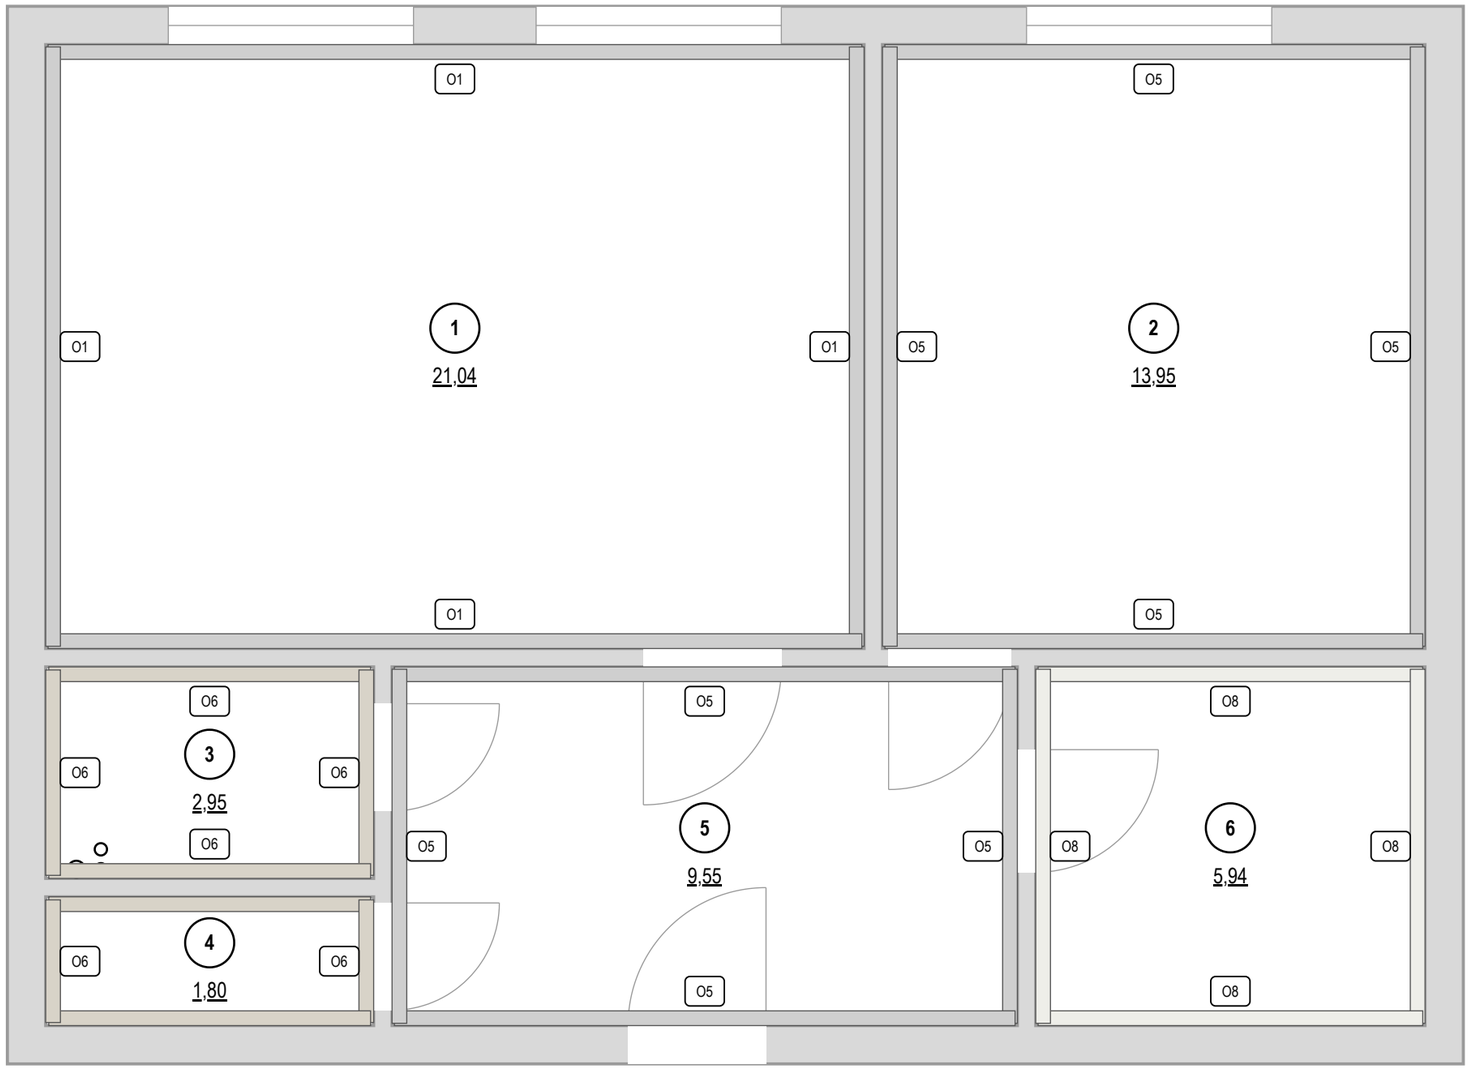

Покрытия стен

Марка	Покрытие	Помещение: S, м²	Итого, м²
О1	окраска Tikkurila · S 1002-Y50R	1: 40,9	40,9
О5	окраска Tikkurila · S 1502-Y50R	2: 34,3; 5: 22,4	56,7
О6	облицовка плиткой Italon · 610015000370 «Charme Extra» 600×1200 мм	3: 16,5; 4: 13,7	30,2
О8	окраска Tikkurila · V503 «Winter»	6: 24,3	24,3

Площади — нетто, по развёрткам (за вычетом проёмов и фартука); высоты помещений — от чистого пола.

	Лист	№ док.	Подпись	Дата
Дизайнер	Кырлан А.С.			04.11.26

Проект: Квартира 58 м² — **М 1:40**

Карта покрытий стен

Стадия	Лист	Листов
П	9	71

Колерная карта по помещениям

Помещение	Поверхность	Образец	Поз.	Система и код цвета	Производитель, линейка / материал, артикул	Блеск	Класс истирания	LRV	Площадь
1. Кухня-гостиная 21,04 м²	стены		**К1**	NCS S 1002-Y50R	Tikkurila	полуматов.	1	82	41,2 м²
	потолок		**К2**	NCS S 0300-N	Tikkurila	глубокомат.	1	92	21,0 м²
	пол		**КМ1**	по образцу	инженерная доска · аналог по хар.				21,0 м²
	плинтус		**К3**	NCS S 0300-N	Orac Decor · Luxxus	полуматов.		92	17,7 м
2. Спальня 13,95 м²	стены		**К4**	NCS S 1502-Y50R	Tikkurila	глубокомат.	2	72	33,9 м²
	потолок		**К5**	NCS S 0300-N	Tikkurila	глубокомат.	2	92	13,9 м²
	пол		**КМ1**	по образцу	инженерная доска · аналог по хар.				13,9 м²
	плинтус		**К3**	NCS S 0300-N	Orac Decor · Luxxus	полуматов.		92	14,2 м
3. Ванная 2,95 м²	стены		**КМ2**	Charme Extra	Italon · арт. 610015000370				16,9 м²
	потолок		**К2**	NCS S 0300-N	Tikkurila	глубокомат.	1	92	3,0 м²
	пол		**КМ3**	Две Венеции / Риальто	Kerama Marazzi · арт. SG651622R				3,0 м²
4. Санузел 1,8 м²	стены		**КМ2**	Charme Extra	Italon · арт. 610015000370				14,1 м²
	потолок		**К2**	NCS S 0300-N	Tikkurila	глубокомат.	1	92	1,8 м²
	пол		**КМ3**	Две Венеции / Риальто	Kerama Marazzi · арт. SG651622R				1,8 м²
5. Прихожая 9,55 м²	стены		**К6**	NCS S 1502-Y50R	Tikkurila	полуматов.	1	72	22,7 м²
	потолок		**К2**	NCS S 0300-N	Tikkurila	глубокомат.	1	92	9,6 м²
	пол		**КМ3**	Две Венеции / Риальто	Kerama Marazzi · арт. SG651622R				9,6 м²
	плинтус		**К3**	NCS S 0300-N	Orac Decor · Luxxus	полуматов.		92	8,0 м
6. Гардеробная 5,94 м²	стены		**К7**	Tikkurila V503	Tikkurila · Harmony	матовая	1	86	24,7 м²
	потолок		**К8**	Tikkurila V503	Tikkurila · Anti-Reflex 2	глубокомат.	2	86	5,9 м²
	пол		**КМ1**	по образцу	инженерная доска · аналог по хар.				5,9 м²
	плинтус		**К9**	Tikkurila V503	Orac Decor · Luxxus			86	9,0 м

Перечень выкрасов на согласование

№	Код	Бренд / веер	Пом. / стена	Подложка	Формат	Статус
1	S 1002-Y50R	NCS Tikkurila	1	ГКЛ с грунтом	600×1000	к выполнению
2	S 0300-N	NCS Tikkurila	1, 2, 3, 4, 5	ГКЛ с грунтом; МДФ под эмаль	600×1000; 300×600	к выполнению
3	S 1502-Y50R	NCS Tikkurila	2, 5	ГКЛ с грунтом	600×1000	к выполнению
4	V503	Tikkurila	6	ГКЛ с грунтом; МДФ под эмаль	600×1000; 300×600	к выполнению

Примечания

1. Цвет на листе и на экране — ориентир. До покраски — выкрас на объекте: не меньше А3 (или лист ГКЛ), на грунте под эту краску, не на белой шпаклёвке, в 2 слоя; на обороте — код, бренд, веер, дата. Смотреть днём и вечером, рядом с образцами пола и плитки; к основному цвету стен — ещё 2 соседних оттенка. Красить только в цвет утверждённого выкраса.
2. Краску заказывать по коду из графы «Система и код цвета» у бренда этого кода, не «аналогом» другого; весь объём одного кода — одной партией, колеруемую краску — за один проход машины.
3. Площади — те же, что в ведомости отделки (лист С1); сколько краски заказать — в спецификации отделочных материалов (лист С2).

Схема квартиры: цвет стен и акценты (б/м)

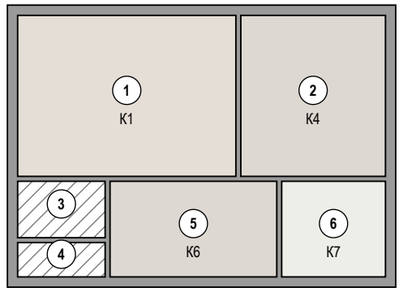


Схема палитры проекта

Стиль: Скандинавский · схема: нейтральная

основной	основной	основной	второстепенный	акцентный
NCS S 1502-Y50R	**NCS S 1002-Y50R**	**NCS S 0300-N**	**Tikkurila V503**	**NCS S 4010-R90B**
тёплый светло-серый LRV 72 стены 2,5	тёплый светлый грейж LRV 82 стены 1	белый LRV 92 потолок 1,2,3,4,5; плинтус 1,2,5	Winter LRV 86 стены 6; потолок 6; плинтус 6	пыльный синий LRV 27 в отделке не применён

План 60/30/10

60%	30%	10%

Окраска, факт — по площади стен, акцентов, потолков

83%	17%

окрашено всего 177,7 м²; второстепенный тон несут мебель и текстиль

Условные обозначения

- **К1** NCS S 1002-Y50R · Tikkurila · полуматов. · кл. 1
- **К2** NCS S 0300-N · Tikkurila · глубокомат. · кл. 1
- **К3** NCS S 0300-N · Orac Decor Luxxus · полуматов.
- **К4** NCS S 1502-Y50R · Tikkurila · глубокомат. · кл. 2
- **К5** NCS S 0300-N · Tikkurila · глубокомат. · кл. 2
- **К6** NCS S 1502-Y50R · Tikkurila · полуматов. · кл. 1
- **К7** Tikkurila V503 · Winter · Harmony · матовая · кл. 1
- **К8** Tikkurila V503 · Winter · Anti-Reflex 2 · глубокомат. · кл. 2
- **К9** Tikkurila V503 · Winter · Luxxus
- **КМ1** аналог: инженерная доска, дуб натуральный, масло, 1-полосная, 14/4 мм
- **КМ2** плитка · 610015000370
- **КМ3** керамогранит · SG651622R

дерево (доска, паркет, ламинат) — рисунок досок


керамогранит, плитка, камень — сетка швов по формату

плашка не залита — цвет только по коду и вееру бренда

К — краска, КМ — отделочный материал (тон КМ — по описанию, эталон — образец материала); кл. — класс истирания (1 — самый стойкий к мытью); LRV — светлота цвета: 0 — чёрный, 100 — белый

	Лист	№ док.	Подпись	Дата	Проект: Квартира 58 м²
Дизайнер	Кырлан А.С.			04.11.26	Колерная карта

Стадия	Лист	Листов
П	10	71

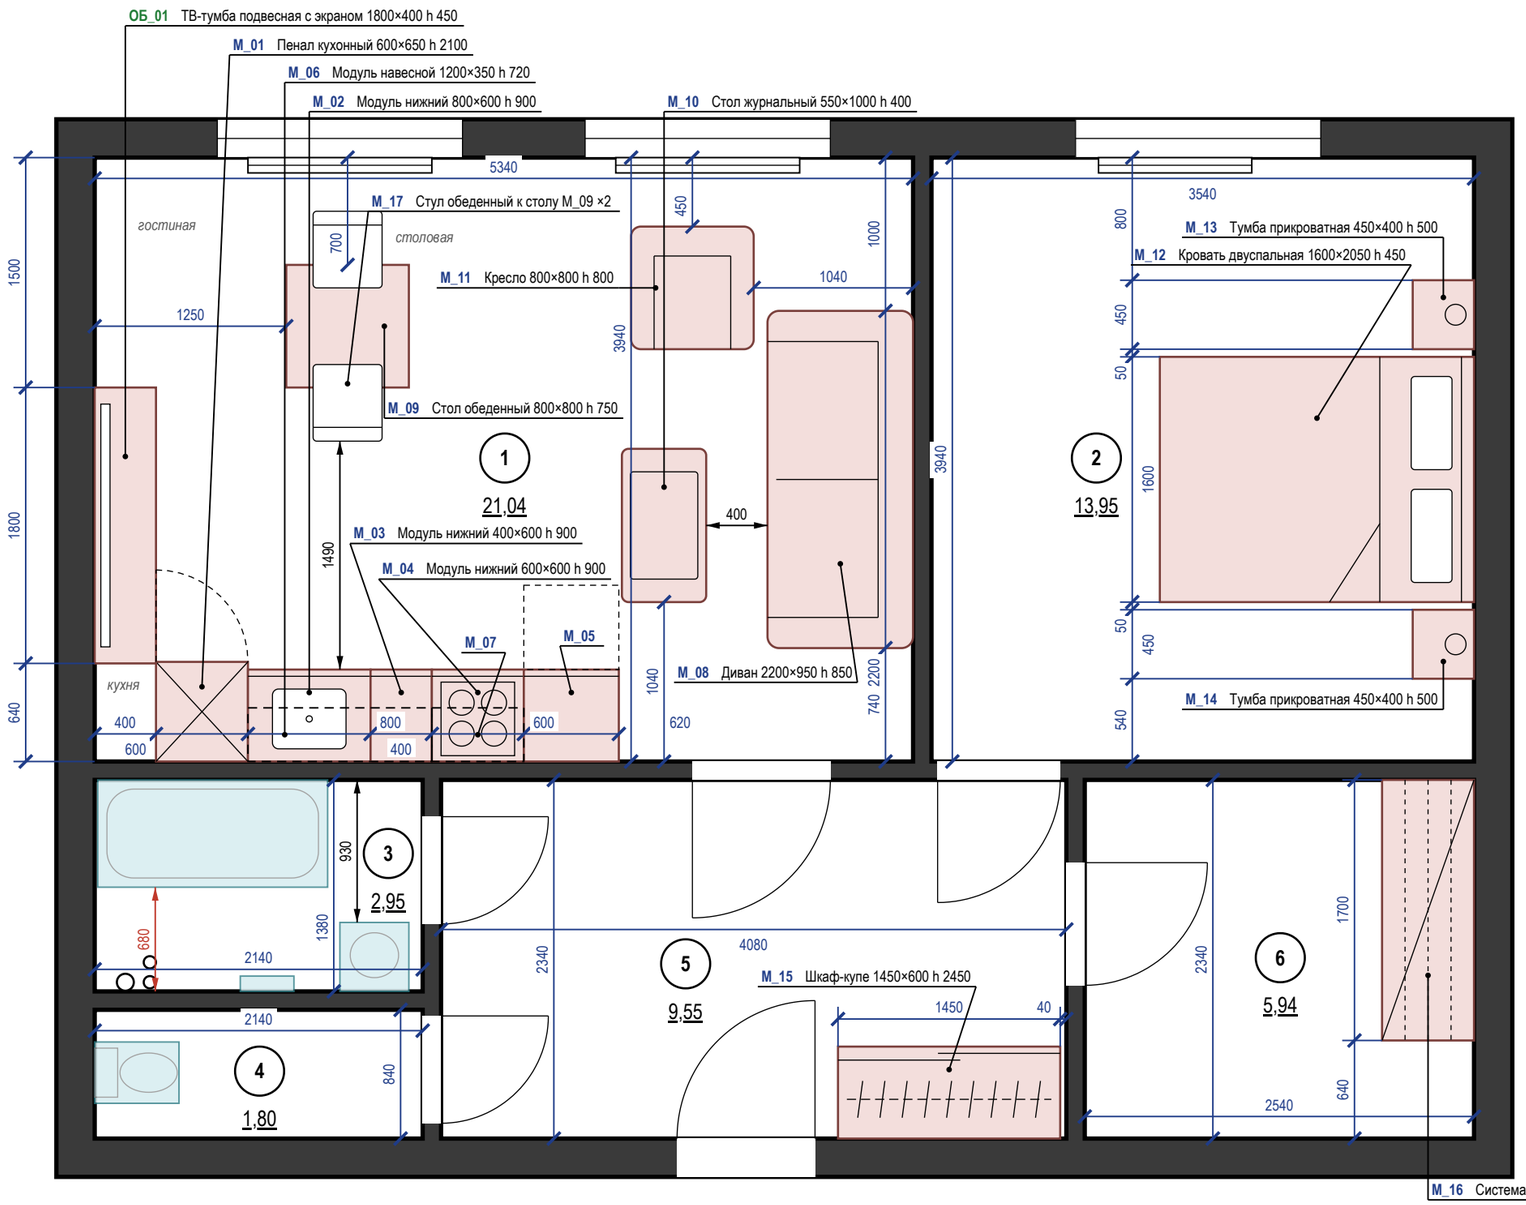

Экспликация помещений

лист 5 · на плане — номера в марках

Ведомость мебели и оборудования

Марка	Наименование	Ш×Г×В, мм	Пом.	Кол.
М_01	Пенал кухонный	600×650×2100	1	1
М_02	Модуль нижний	800×600×900	1	1
М_03	Модуль нижний	400×600×900	1	1
М_04	Модуль нижний	600×600×900	1	1
М_05	Ниша под стиральную машину	620×600×900	1	1
М_06	Модуль навесной	1200×350×720	1	1
М_07	Навесной модуль над варочной	600×350×620	1	1
М_08	Диван	2200×950×850	1	1
М_09	Стол обеденный	800×800×750	1	1
ОБ_01	ТВ-тумба подвесная с экраном	1800×400×450	1	1
М_10	Стол журнальный	550×1000×400	1	1
М_11	Кресло	800×800×800	1	1
М_12	Кровать двуспальная	1600×2050×450	2	1
М_13	Тумба прикроватная	450×400×500	2	1
М_14	Тумба прикроватная	450×400×500	2	1
М_15	Шкаф-купе	1450×600×2450	5	1
М_16	Система хранения	1700×600×2400	6	1
М_17	Стул обеденный к столу М_09	450×500×820	1	2

Ш — вдоль стены (изголовья), Г — от стены (длина кровати)

Материалы, модели, допуск замены — лист 12

Примечания

1. Размеры — в мм от чистовых поверхностей стен; размеры мебели уточнить после отделочных работ; общие указания — лист 3.
2. У позиций М_05, М_07 на плане только марка: наименование и габарит — в спецификации, лист 12.
3. Стулья обеденной группы (М_17 — 2 шт.) показаны в рабочем положении, задвинутыми под столешницу на 150 мм.

					Проект: Квартира 58 м²	М 1:40
	Лист	№ док.	Подпись	Дата		
Дизайнер	Кырлан А.С.			04.11.26	План размещения мебели и оборудования	Стадия: П; Лист: 11; Листов: 71

Поз.	Наименование и техническая характеристика	Тип, марка, обозначение документа, опросного листа	Код продукции	Поставщик	Ед. измерения	Кол.	Масса 1 ед., кг	Примечание
	Мебель встроенная и корпусная (изготовление по чертежам мебельщика)							
M_01	Пенал кухонный, холодильник; корпус ЛДСП 16 мм; фасады — без фасада (прибор отдельностоящий); Ш×Г×В 600×650×2100 мм			изготовление на заказ	шт.	1		пом. 1
M_02	Модуль нижний, мойка; корпус ЛДСП 16 мм; фасады — МДФ эмаль 18 мм; Ш×Г×В 800×600×900 мм			изготовление на заказ	шт.	1		пом. 1
M_03	Модуль нижний; корпус ЛДСП 16 мм; фасады — МДФ эмаль 18 мм; Ш×Г×В 400×600×900 мм			изготовление на заказ	шт.	1		пом. 1
M_04	Модуль нижний, варочная; корпус ЛДСП 16 мм; фасады — МДФ эмаль 18 мм; Ш×Г×В 600×600×900 мм			изготовление на заказ	шт.	1		пом. 1
M_05	Модуль под встраиваемую ПММ 60; без корпуса (ниша между соседними модулями); фасад на дверь машины — МДФ эмаль 18 мм; цоколь; Ш×Г×В 620×600×900 мм			изготовление на заказ	шт.	1		пом. 1
M_06	Модуль навесной; корпус ЛДСП 16 мм; фасады — МДФ эмаль 18 мм; Ш×Г×В 1200×350×720 мм			изготовление на заказ	шт.	1		пом. 1
M_07	Навесной модуль над варочной, вытяжка встраивается в дно; корпус ЛДСП 16 мм; фасады — МДФ эмаль 18 мм; Ш×Г×В 600×350×620 мм			изготовление на заказ	шт.	1		пом. 1
M_15	Шкаф-купе; корпус ЛДСП 16 мм; фасады — ЛДСП 10 мм в алюминиевом профиле; Ш×Г×В 1450×600×2450 мм			изготовление на заказ	шт.	1		пом. 5
M_16	Система хранения: штанги, полки, ящики; каркас и полки — ЛДСП 16 мм, декор «дуб натуральный»; без фасадов; Ш×Г×В 1700×600×2400 мм			изготовление на заказ	шт.	1		пом. 6; крепление к стене
	Мебель покупная							
M_08	Диван; обивка — ткань, цвет Tikkurila V503; Ш×Г×В 2200×950×850 мм			аналог по характеристикам	шт.	1		пом. 1; замена ≤ габарита
M_09	Стол обеденный; шпон, дуб натуральный, матовое масло; Ш×Г×В 800×800×750 мм			аналог по характеристикам	шт.	1		пом. 1; замена ≤ габарита
M_10	Стол журнальный; шпон, дуб натуральный, матовое масло; Ш×Г×В 550×1000×400 мм			аналог по характеристикам	шт.	1		пом. 1; замена ≤ габарита
M_11	Кресло; обивка — ткань, цвет Tikkurila V503; Ш×Г×В 800×800×800 мм			аналог по характеристикам	шт.	1		пом. 1; замена ≤ габарита
M_17	Стул обеденный к столу M_09; обивка — ткань, цвет Tikkurila V503; каркас — дуб натуральный; Ш×Г×В 450×500×820 мм			аналог по характеристикам	шт.	2		пом. 1; замена ≤ габарита
ОБ_01	ТВ-тумба подвесная с экраном; шпон, дуб натуральный, матовое масло; Ш×Г×В 1800×400×450 мм			аналог по характеристикам	шт.	1		пом. 1; замена ≤ габарита
M_12	Кровать двуспальная; мягкое изголовье, обивка — ткань, цвет Tikkurila V503; Ш×Г×В 1600×2050×450 мм			аналог по характеристикам	шт.	1		пом. 2; замена ≤ габарита
M_13, M_14	Тумба прикроватная; шпон, дуб натуральный, матовое масло; Ш×Г×В 450×400×500 мм			аналог по характеристикам	шт.	2		пом. 2; замена ≤ габарита
	Техника встраиваемая и бытовая (покупные изделия), светильники под розетки							
	Холодильник, в модуле M_01	аналог по характеристикам: отдельностоящий, габарит — по проёму		по выбору заказчика до изготовления мебели	шт.	1		пом. 1; по схеме изготовителя
	Варочная панель встраиваемая, индукционная, в модуле M_04	аналог по характеристикам: индукционная 60 см, вырез 560 × 490 мм по шаблону модели		по выбору заказчика до изготовления мебели	шт.	1		пом. 1; по схеме изготовителя
	Стиральная машина, в модуле M_05	аналог по характеристикам: тип загрузки — по листу ВК, по листу ВК		по выбору заказчика до изготовления мебели	шт.	1		пом. 1; по схеме изготовителя
	Вытяжка встраиваемая, в модуле M_07	аналог по характеристикам: производительность — по расчёту ОВ, шум ≤ 55 дБ(А)		по выбору заказчика до изготовления мебели	шт.	1		пом. 1; по схеме изготовителя
	Торшер, у поз. M_09; абажур — ткань или опаловое стекло; лампа 3000 K			аналог по характеристикам	шт.	1		пом. 1; розетка — по плану розеток (ЭОМ)

Примечания

1. Позиции мебели совпадают с марками на плане расстановки; размеры Ш×Г×В — Ш вдоль стены, Г от стены.
2. Размеры и привязки плана расстановки — в мм от чистовых поверхностей стен: слой штукатурки 20 мм по блоку и 5 мм шпаклёвки по ГКЛ учтён; привязки — от стен и углов помещения, а не от другой мебели.
3. План расстановки не является документацией для изготовления мебели. Встроенная и корпусная мебель изготавливается по чертежам мебельщика после контрольного обмера (после штукатурки); «стена в стену» — с зазором 10 мм с каждой стороны или с компенсаторами; графы «Тип, марка» и «Код продукции» для неё не заполняются (ГОСТ 21.110-2013).
4. Покупные изделия — аналог по характеристикам: заменять только на изделия не больше указанного габарита и того же материала и цвета.
5. Материал и цвет, не указанные в данных изделия, приняты по концепции: тон дерева — по полу, обивка — по вторичному цвету палитры; образцы согласовать до заказа.
6. Масса 1 ед. для изделий до 25 кг не указывается. Техника — по монтажным схемам изготовителя; выводы — по листам ЭОМ и ВК.

					Проект: Квартира 58 м²
	Лист	№ док.	Подпись	Дата	Спецификация мебели и оборудования
Дизайнер	Кырлан А.С.			04.11.26	

Стадия	Лист	Листов
П	12	71

Ведомость изделий

Марка	Наименование	Пом.	Ш×Г×В, мм	Корпус	Фасад	Кромка, мм	Кол.
M_15	Шкаф-купе	5	1450×600×2450	ЛДСП 16	ЛДСП 10 мм в алюминиевом профиле	0,4 / 1	1
M_16	Система хранения	6	1700×600×2400	ЛДСП 16	без фасадов	0,4 / 2	1
M_05	Ниша под стиральную машину 620: без корпуса, между боковинами соседних модулей, фасад на петлях к боковине соседнего модуля; цоколь съёмный	1	620×600×900	без корпуса	МДФ эмаль 18 мм — на дверь машины (навеска из её комплекта), цоколь		1
M_04	Модуль нижний: ящики, варочная	1	600×600×900	ЛДСП 16	МДФ эмаль 18 мм	0,4 / 1	1
M_07	Модуль навесной: полки	1	600×350×620	ЛДСП 16	МДФ эмаль 18 мм	0,4 / 1	1
M_03	Модуль нижний: ящики	1	400×600×900	ЛДСП 16	МДФ эмаль 18 мм	0,4 / 1	1
M_06	Модуль навесной: полки, сушка	1	1200×350×720	ЛДСП 16	МДФ эмаль 18 мм	0,4 / 1	1
M_02	Модуль нижний: мойка	1	800×600×900	ЛДСП 16	МДФ эмаль 18 мм	0,4 / 1	1
M_01	Место под холодильник отдельностоящий: без корпуса и фасада	1	600×650×2100 (место в ряду)	без корпуса	без фасада (прибор отдельностоящий)		

Ведомость встраиваемой техники

Поз.	Прибор	Ниша, вырез, мм	Вентиляция	Питание	Схема
M_04	Варочная панель индукционная, 60 см	вырез в столешнице 560 × 490		M_04, H=150 — в соседнем модуле, за ящиком	по модели
M_02	Мойка врезная / подстольная с сифоном	вырез по шаблону, ориентир 700 × 480		смеситель — выводы ВК	по модели
M_01	Холодильник отдельностоящий	проём 600, зазор сверху ≥ 50	по паспорту модели	питание: точка ЭОМ не задана — вывод под прибор не делать до задания	по модели
M_07	Вытяжка встраиваемая в навесной модуль, 60 см	низ ≥ 650 над панелью	воздуховод к вентканалу, короб до потолка	питание: точка ЭОМ не задана — вывод под прибор не делать до задания	по модели

Ведомость фурнитуры

№	Фурнитура	Тип, размер	Изделия	Кол.
1	Система дверей купе: профиль, направляющие, ролики	на 2 двери	M_15	1
2	Ручка-профиль вертикальная	в цвет профиля	M_15	2
3	Полкодержатель с фиксацией	ø5 мм	M_15, M_16, M_07, M_06	56
4	Штанга овальная 30×15, L = 701	+ 2 держателя	M_15	1
5	Полка для обуви выдвижная наклонная	ширина 701	M_15	3
6	Опора регулируемая с цоколем на клипсах	ход 20 мм	M_15, M_16	14
7	Анкер по основанию стены	по таблице крепежа	M_15, M_16, M_07, M_06	20
8	Уголок крепления к стене от опрокидывания	стальной	M_15, M_16	4
9	Штанга овальная 30×15, L = 545	+ 2 держателя	M_16	3
10	Петля накладная 110° с доводчиком	чашка 35 мм	M_05, M_07, M_06, M_02	16
11	Ручка-профиль	латунь матовая	M_05, M_04, M_07, M_03, M_06, M_02	14
12	Направляющие полного выдвижения с доводчиком NL 500	пара	M_04, M_03	6
13	Опора кухонная регулируемая 100–120 мм	+ клипса цоколя	M_04, M_03, M_02	14
14	Навес регулируемый для навесного шкафа	пара на секцию	M_07, M_06	3
15	Шина монтажная	L = 540	M_07	1
16	Сушка для посуды в шкаф	ширина 800	M_06	1
17	Шина монтажная	L = 1140	M_06	1

Примечания


1. Модели техники выбирает заказчик до изготовления мебели; ниши, вырезы и вентиляция — по монтажной схеме выбранной модели (условие гарантии), её номер вносится в ведомость.
2. Количество фурнитуры — по чертежам изделий; запас крепежа 5 %. Аналоги — по характеристикам (доводчик, нагрузка, ход).
3. Цвет корпусов, фасадов и профилей — по колерной карте проекта. Кромка — скрытые / видимые торцы, мм.

					Проект: Квартира 58 м²
	Лист	№ док.	Подпись	Дата	
Дизайнер	Кырлан А.С.			04.11.26	Ведомости изделий, техники и фурнитуры


Стадия	Лист	Листов
П	13	71

выпуск 04.11.2026 № e0dc2f2b59 · стр. 13 из 71


Фрагмент 1. Кухня-гостиная (пом. 1)

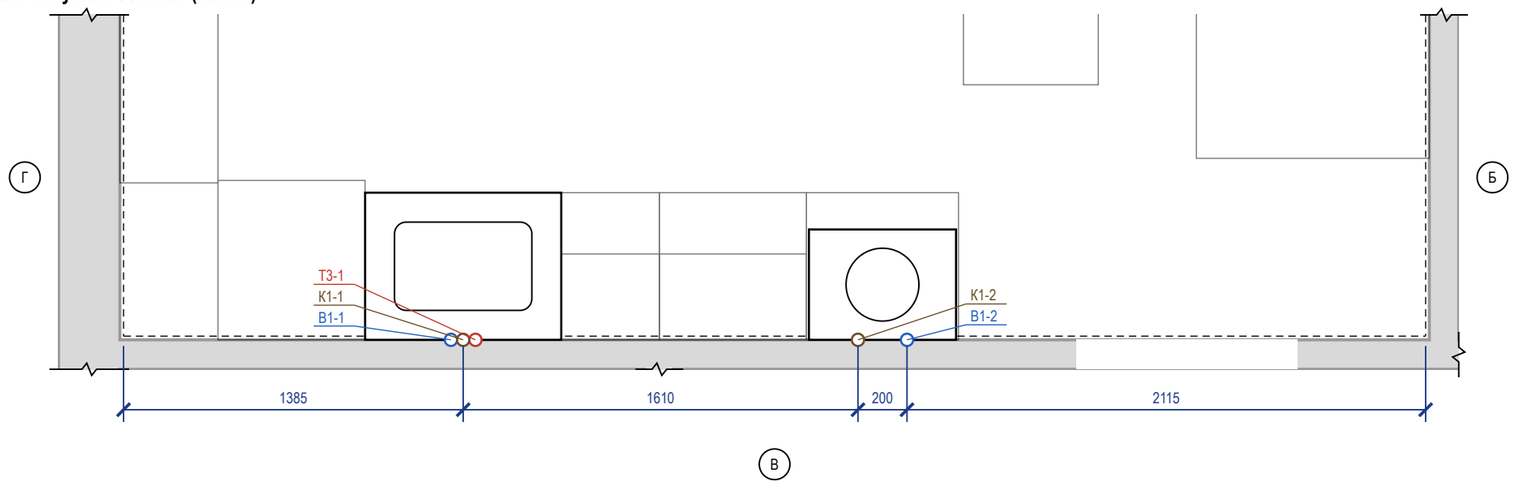

Фрагмент 2. Ванная (пом. 3)

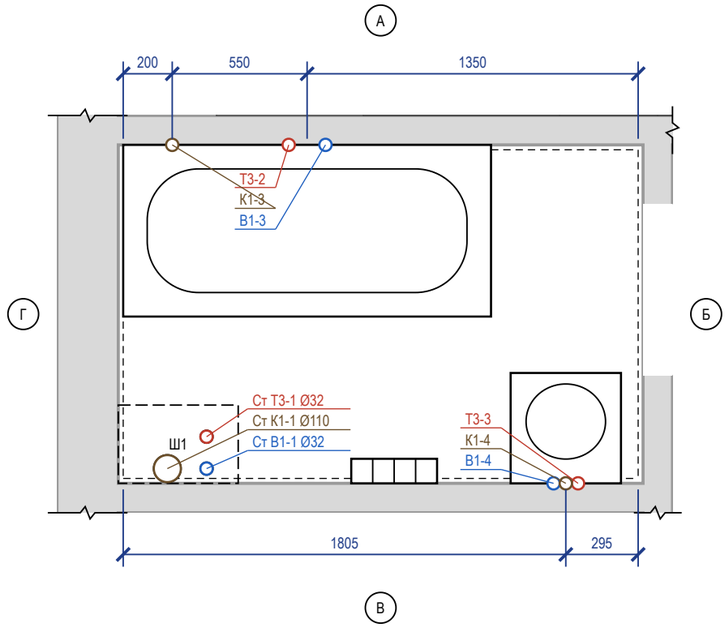

Фрагмент 3. Санузел (пом. 4)

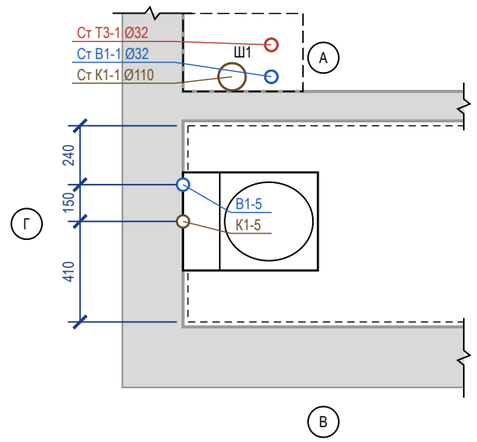

Ведомость привязок выводов

Код	Прибор	Ø	H, мм	Привязка от чист. стен, мм	Прим.
В1-1	С_01 мойка кухонная	½"	550	ст. В: 1335 от Г	межос. 100
Т3-1	С_01 мойка кухонная	½"	550	ст. В: 1435 от Г	межос. 100
К1-1	С_01 мойка кухонная	Ø50	400	ст. В: 1385 от Г	
В1-2	ОБ_02 стиральная машина	½"	600	ст. В: 2115 от Б	кран машины
К1-2	ОБ_02 стиральная машина	Ø40	600	ст. В: 2315 от Б	
В1-3	С_02 ванна	½"	800	ст. А: 825 от Г	межос. 150
Т3-2	С_02 ванна	½"	800	ст. А: 675 от Г	межос. 150
К1-3	С_02 ванна	Ø50	50	ст. А: 200 от Г	
В1-4	С_03 умывальник	½"	550	ст. В: 345 от Б	межос. 100
Т3-3	С_03 умывальник	½"	550	ст. В: 245 от Б	межос. 100
К1-4	С_03 умывальник	Ø50	500	ст. В: 295 от Б	
В1-5	С_05 унитаз подвесной	½"	150	ст. Г: 240 от А	в раме инсталляции
К1-5	С_05 унитаз подвесной	Ø110	230	ст. Г: 390 от А	

Условные обозначения

- вывод В1 (код — в ведомости привязок)
- вывод Т3 (код — в ведомости привязок)
- вывод К1 (код — в ведомости привязок)
- сантехприбор по расстановке (габарит модели)
- чистовая поверхность стены (от неё привязки)
- стояк «Ст К1-N / Ст В1-N» (ГОСТ 21.601), Ø мм
- шахта / короб стояков, люк 300×400
- линия обрыва (граница фрагмента)
- А — обозначение стены А–Г (как на развёртках)


Примечания

1. Привязки выводов даны от чистовых поверхностей стен (облицовка на сторону: кухня-гостиная — 15 мм (по данным); ванная — 20 мм (по данным); санузел — 20 мм (по данным)); эти же грани — на развёртках и в раскладке плитки. Высоты — от чистого пола помещения.
2. До черновой разводки сверить по паспорту выбранного прибора (смеситель, инсталляция, сифон).
3. Горячая вода (Т3) — слева от холодной (В1), если смотреть на прибор. Допуск установки выводов: ±5 мм в группе, ±20 мм у отдельно стоящих.
4. Расчёт систем водоснабжения и канализации и подбор оборудования выполняет проектная организация; лист задаёт места и высоты выводов.
5. Стояки в коробах/шахтах Ш1 не замоноличивать; стояк К1 в коробе — звукоизоляция стояка в коробе без жёсткого контакта с трубой; к арматуре и ревизиям — люк не меньше 300×400.


					Проект: Квартира 58 м² — М 1:25
	Лист	№ док.	Подпись	Дата	План выводов сантехники
Дизайнер	Кырлан А.С.			04.11.26	Стадия: П; Лист: 14; Листов: 71

выпуск 04.11.2026 № e0dc2f2b59 · стр. 14 из 71


План квартиры (М 1:200)

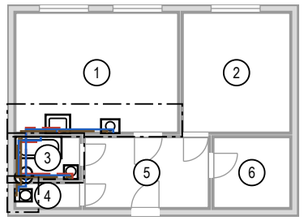


Фр. 1. Кухня-гостиная (М 1:25)

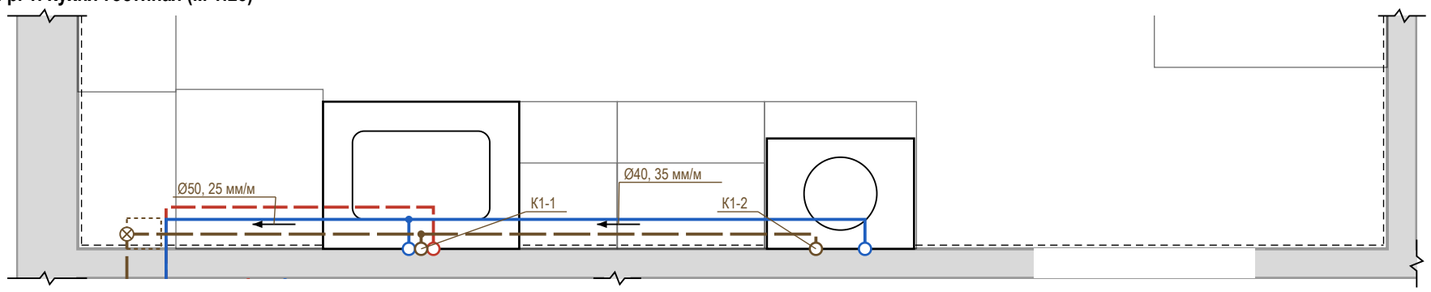

Фр. 2. Ванная (М 1:25)

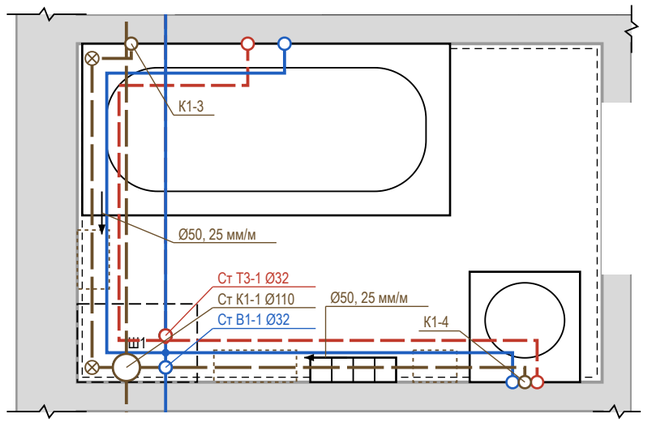

Фр. 3. Санузел (М 1:25)

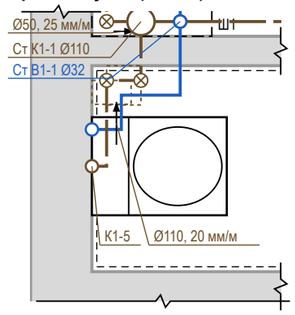

Условные обозначения

- В1 — водопровод хозяйственно-питьевой (ХВС), PP-R Ø20
- Т3 — горячее водоснабжение, подача (ГВС), PP-R Ø20
- К1 — канализация бытовая
- направление уклона К1 / пола: Ø, мм на 1 м
- ревизия (прочистка) К1 — доступ сохранить
- тройник (ответвление к прибору)
- короб К1 над чистым полом (ГКЛВ под плитку)
- вывод В1 (код — в ведомости привязок)
- вывод Т3 (код — в ведомости привязок)
- вывод К1 (код — в ведомости привязок)
- сантехприбор по расстановке (габарит модели)
- стояк «Ст К1-N / Ст В1-N» (ГОСТ 21.601), Ø мм
- шахта / короб стояков, люк 300×400
- линия обрыва (граница фрагмента)
- граница фрагмента на плане (Фр. N)

Профиль выпусков К1 (до врезки в стояк)

Выпуск	Прибор	Ø	L, м	i, мм/м	Δh, мм	Прокладка, мм
К1-5	С_05 унитаз подвесной	Ø110	0,79	20	16	короб 160×140
К1-1	С_01 мойка кухонная	Ø50	2,76	25	69	короб 150×110
К1-4	С_03 умывальник	Ø50	1,69	25	42	короб 130×110
К1-3	С_02 ванна	Ø50	1,62	25	41	короб 130×110
К1-2	ОБ_02 стиральная машина	Ø40	4,37	35	153	короб 230×110

Короб h×b: h — от чистого пола, b — от чистовой стены. Стяжка 90 мм — лист полов.

Узел ввода В1, Т3 (схема, без масштаба)



состав узла — по согласованию


⊗ Ст К1-1: ревизия на стояке — люк в коробе

Примечания

1. Трассы принципиальные, построены от стояков вдоль стен помещений; фактическое положение фиксируется исполнительной схемой с привязками (фото с рулеткой) до закрытия.
2. Уклон К1 не менее 1/d и не более 150 мм/м (СП 30.13330.2020, п. 19.1), приняты практические уклоны; поворот — двумя отводами 45°, ревизия после поворота, доступ сохранить. Стояк К1 в коробе — звукоизоляция стояка в коробе, без жёсткого контакта короба с трубой.
3. Решение по К1: стяжка 90 мм не укрывает трубы (нужно Ø + Δh + 45 мм) — выпуски идут над чистым полом вдоль стен; К1-5, К1-1, К1-4, К1-3, К1-2 — в коробе ГКЛВ под плитку (размеры в профиле). Короба — на развёртках; отметку низа врезки в стояк замерить до черновых работ.
4. Отводы К1-2 (4,4 м) длиннее 4 м без вентиляции — у прибора воздушный клапан Ø50 в доступном месте (за люком или в тумбе) либо вентилируемый отвод (EN 12056-2, табл. 4), подбор — проектная организация.
5. Состав узла ввода В1, Т3 — по согласованию: на схеме типовой узел — кран шаровой, фильтр, счётчик, обратный клапан, кран; состав и места не определены (записи реестра нет). Доступ к арматуре — через люк не меньше 300×400. Водопровод — в штробе стен или в коробах; трубы испытать давлением до закрытия (акт скрытых работ).
6. Расчёт систем, диаметры магистралей и подбор оборудования выполняет проектная организация; врезка и перенос стояков — по согласованию с управляющей организацией. Арматуру и привязки сверить по паспортам приборов.

					Проект: Квартира 58 м²
	Лист	№ док.	Подпись	Дата	
Дизайнер	Кырлан А.С.			04.11.26	Схема разводки водопровода и канализации
					Стадия: П; Лист: 15; Листов: 71

Схема В1 (М 1:50; по вертикали и горизонтали один масштаб, глубина — ×0,5 под 45°)

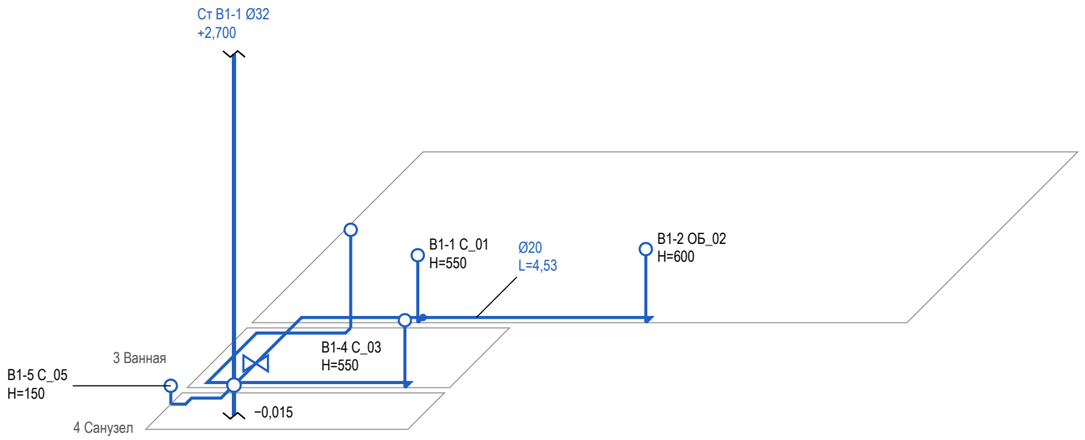

Условные обозначения


- В1 — водопровод хозяйственно-питьевой (ХВС), PP-R Ø20
- вывод В1 (код — в ведомости привязок)
- стояк «Ст К1-N / Ст В1-N» (ГОСТ 21.601), Ø мм
- стояк в плане (на отметке пола); вертикаль — стояк по высоте, разрыв — перекрытие
- тройник (ответвление к прибору)
- кран шаровой

Примечания

1. Схема В1 построена по тем же трассам, что план разводки: положение в плане сохранено, глубина — в масштабе ×0,5. Трассы принципиальные; фактическое положение фиксируется исполнительной схемой до закрытия.
2. Высоты Н — от чистого пола помещения, мм. Отметка прокладки магистрали В1 (в стяжке, в стене или по полу) в данных не задана: участки показаны на уровне пола условно (записи реестра нет).
3. Узел ввода В1 (кран, фильтр, счётчик, обратный клапан, кран) — на схеме разводки; состав узла ввода — по согласованию. Кран шаровой — на первом участке от стояка.
4. Трубы испытать давлением до закрытия (акт скрытых работ, опрессовка по СП 73.13330.2016).
5. Диаметры, высоты выводов и места кранов — по паспортам выбранных приборов и расчёту проектной организации.
6. Расчёт систем, диаметры магистралей и подбор оборудования выполняет проектная организация.

					Проект: Квартира 58 м²	М 1:50
	Лист	№ док.	Подпись	Дата	Аксонометрическая схема В1 (холодное водоснабжение)	Стадия / Лист / Листов
Дизайнер	Кырлан А.С.			04.11.26		П / 16 / 71

Схема Т3 (М 1:50; по вертикали и горизонтали один масштаб, глубина — ×0,5 под 45°)

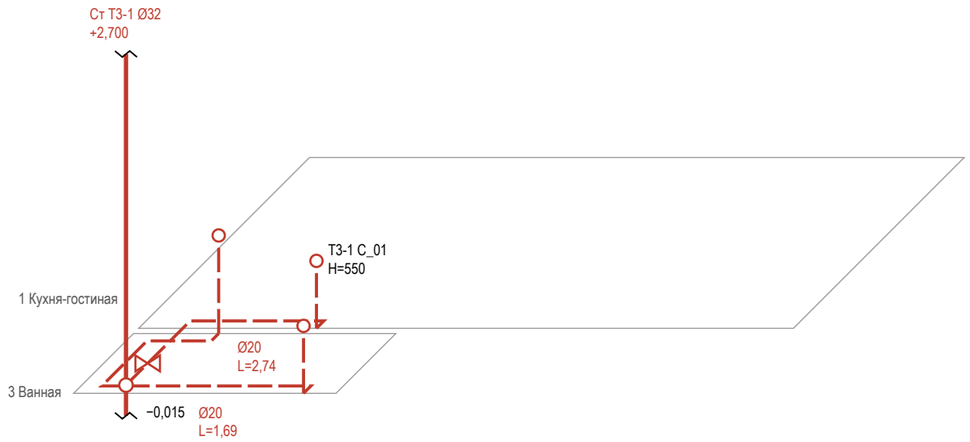

Условные обозначения


- Т3 — горячее водоснабжение, подача (ГВС), PP-R Ø20
- вывод Т3 (код — в ведомости привязок)
- стояк «Ст К1-N / Ст В1-N» (ГОСТ 21.601), Ø мм
- стояк в плане (на отметке пола); вертикаль — стояк по высоте, разрыв — перекрытие
- тройник (ответвление к прибору)
- кран шаровой

Примечания

1. Схема Т3 построена по тем же трассам, что план разводки: положение в плане сохранено, глубина — в масштабе ×0,5. Трассы принципиальные; фактическое положение фиксируется исполнительной схемой до закрытия.
2. Высоты Н — от чистого пола помещения, мм. Отметка прокладки магистрали Т3 (в стяжке, в стене или по полу) в данных не задана: участки показаны на уровне пола условно (записи реестра нет).
3. Узел ввода Т3 (кран, фильтр, счётчик, обратный клапан, кран) — на схеме разводки; состав узла ввода — по согласованию. Кран шаровой — на первом участке от стояка.
4. Циркуляция ГВС в данных не задана — циркуляционного трубопровода на схеме нет (записи реестра нет).
5. Трубы испытать давлением до закрытия (акт скрытых работ, опрессовка по СП 73.13330.2016).
6. Диаметры, высоты выводов и места кранов — по паспортам выбранных приборов и расчёту проектной организации.
7. Расчёт систем, диаметры магистралей и подбор оборудования выполняет проектная организация.

					Проект: Квартира 58 м²	М 1:50
	Лист	№ док.	Подпись	Дата	Аксонометрическая схема Т3 (горячее водоснабжение)	Стадия / Лист / Листов
Дизайнер	Кырлан А.С.			04.11.26		П / 17 / 71

Схема К1 (М 1:50; по вертикали и горизонтали один масштаб, глубина — ×0,5 под 45°)

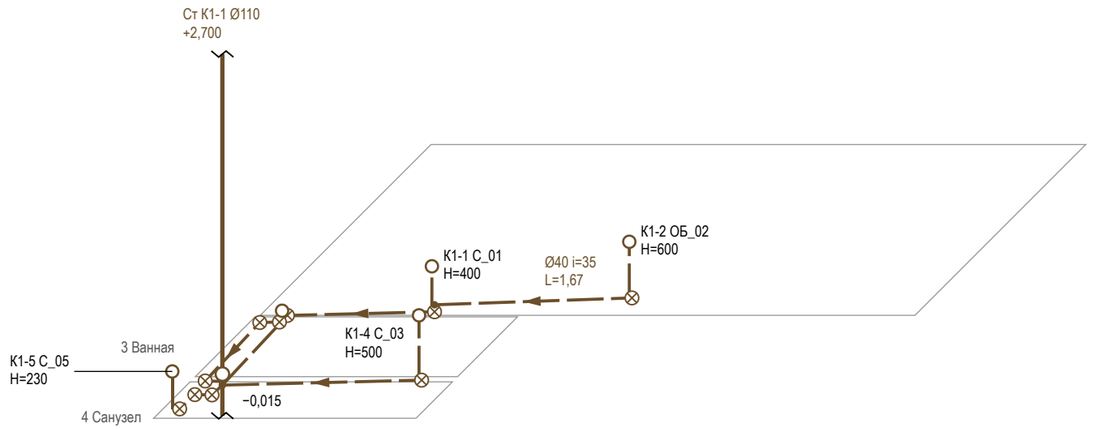

Условные обозначения


- К1 — канализация бытовая
- вывод К1 (код — в ведомости привязок)
- стояк «Ст К1-N / Ст В1-N» (ГОСТ 21.601), Ø мм
- стояк в плане (на отметке пола); вертикаль — стояк по высоте, разрыв — перекрытие
- направление уклона К1 / пола: Ø, мм на 1 м
- ревизия (прочистка) К1 — доступ сохранить
- тройник (ответвление к прибору)

Примечания

1. Схема К1 построена по тем же трассам, что план разводки: положение в плане сохранено, глубина — в масштабе ×0,5. Трассы принципиальные; фактическое положение фиксируется исполнительной схемой до закрытия.
2. Отметки — от плиты перекрытия: низ трубы у врезки в стояк — отметка из данных выпуска, к прибору труба поднимается на уклон i, мм/м (уклон не менее 1/d и не более 150 мм/м, СП 30.13330.2020, п. 19.1); чистый пол — выше плиты на стяжку (высота пирога пола). Высота выпуска прибора H — от чистого пола.
3. Ревизия — на повороте и в начале участка; стояк К1 в коробе с люком — звукоизоляция стояка в коробе; поворот — двумя отводами 45°.
4. Трубы испытать давлением до закрытия (акт скрытых работ, опрессовка по СП 73.13330.2016).
5. Диаметры, высоты выводов и места кранов — по паспортам выбранных приборов и расчёту проектной организации.
6. Расчёт систем, диаметры магистралей и подбор оборудования выполняет проектная организация.

					Проект: Квартира 58 м²	М 1:50
	Лист	№ док.	Подпись	Дата		
Дизайнер	Кырлан А.С.			04.11.26	Аксонометрическая схема К1 (канализация)	
					Стадия: П	Лист: 18 / Листов: 71

Стена В (М 1:20)

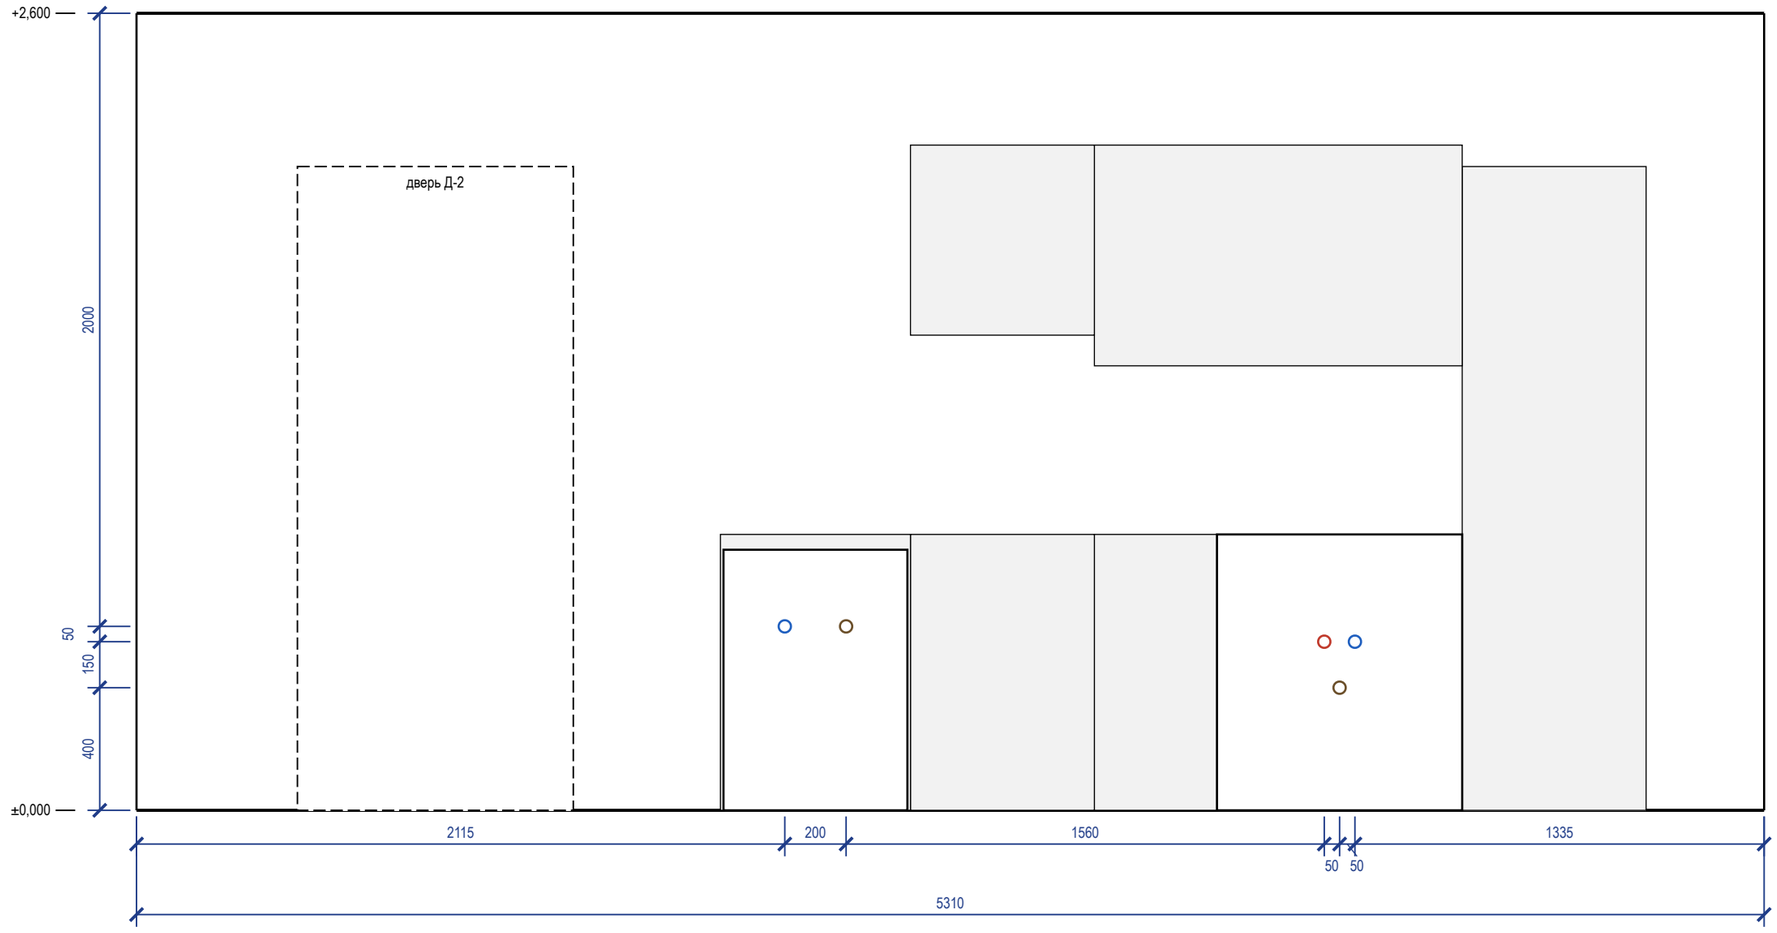

Ведомость привязок выводов (от чистого пола и угла)

Код	Прибор	Ø	H, мм	Привязка, мм
В1-1	С_01 мойка кухонная	½"	550	ст. В: 3975 от лев. угла
Т3-1	С_01 мойка кухонная	½"	550	ст. В: 3875 от лев. угла
К1-1	С_01 мойка кухонная	Ø50	400	ст. В: 3925 от лев. угла
В1-2	ОБ_02 стиральная машина	½"	600	ст. В: 2115 от лев. угла
К1-2	ОБ_02 стиральная машина	Ø40	600	ст. В: 2315 от лев. угла

Условные обозначения


- вывод В1 (код — в ведомости привязок)
- вывод Т3 (код — в ведомости привязок)
- вывод К1 (код — в ведомости привязок)
- сантехприбор по расстановке (габарит модели)
- дверной проём; окно — сплошной контур

Примечания


1. Габариты и высоты приборов, межосевые смесителей и места кранов — по паспортам выбранных приборов, сверяются до разметки стен.
2. Высоты H — от чистого пола помещения, мм; отметка чистого пола и потолка — у левого края вида (от ±0,000 объекта). Привязки — от левого чистового угла вида (облицовка стен вычтена), как на развёртках стен.
3. Ревизионные люки к арматуре и ревизиям в данных не заданы: место и размер не определены (записи реестра нет).
4. Мойка, ПММ и фильтр — выводы в шкафу мойки; диаметры и положение сифона и кранов сверить по паспортам приборов и чертежам модуля.
5. Часть подписей выводов не уместилась у знака: коды и высоты — в ведомости привязок.
6. Расчёт систем водоснабжения и канализации и подбор оборудования выполняет проектная организация; лист задаёт места и высоты выводов.

					Проект: Квартира 58 м²	М 1:20
	Лист	№ док.	Подпись	Дата		
Дизайнер	Кырлан А.С.			04.11.26	Развёртки мокрых зон: выводы ВК. Кухня-гостиная	Стадия: П; Лист: 19; Листов: 71


Стена А (М 1:20)

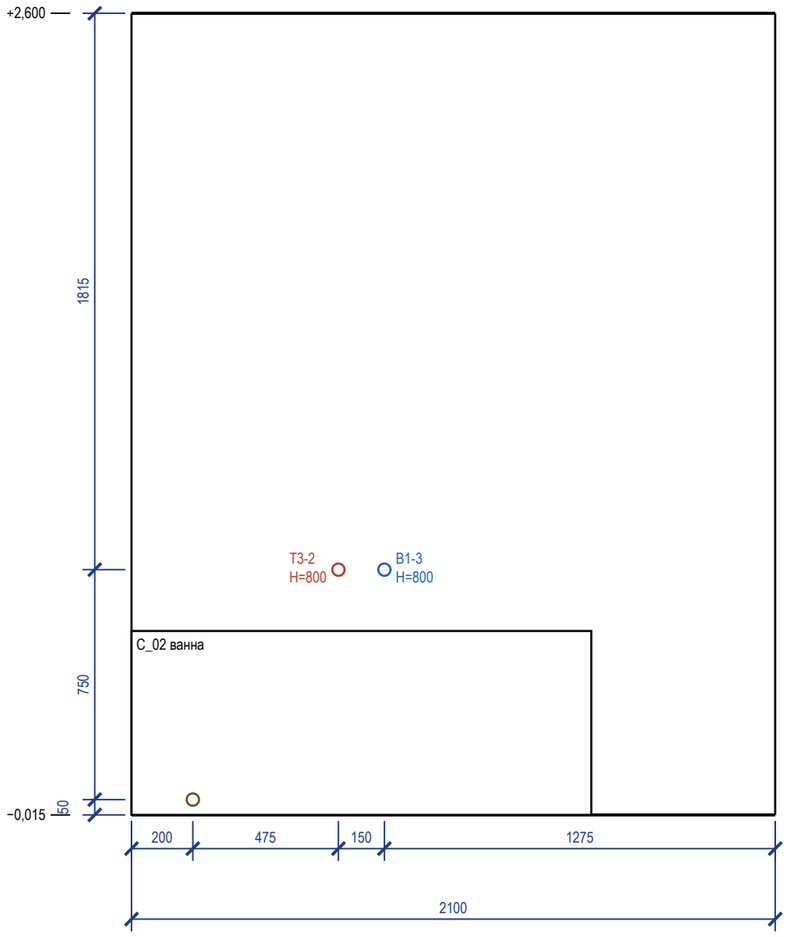

Стена Б (М 1:20)

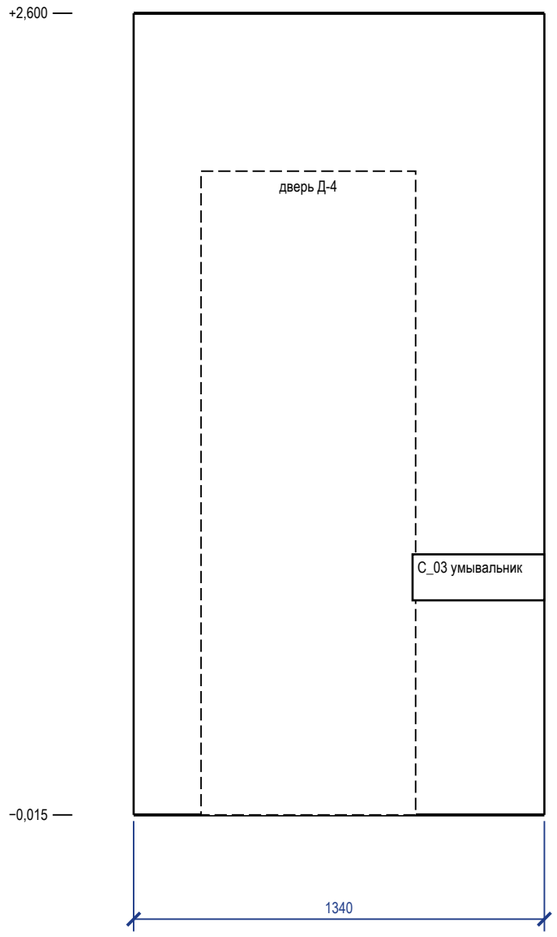

Стена В (М 1:20)

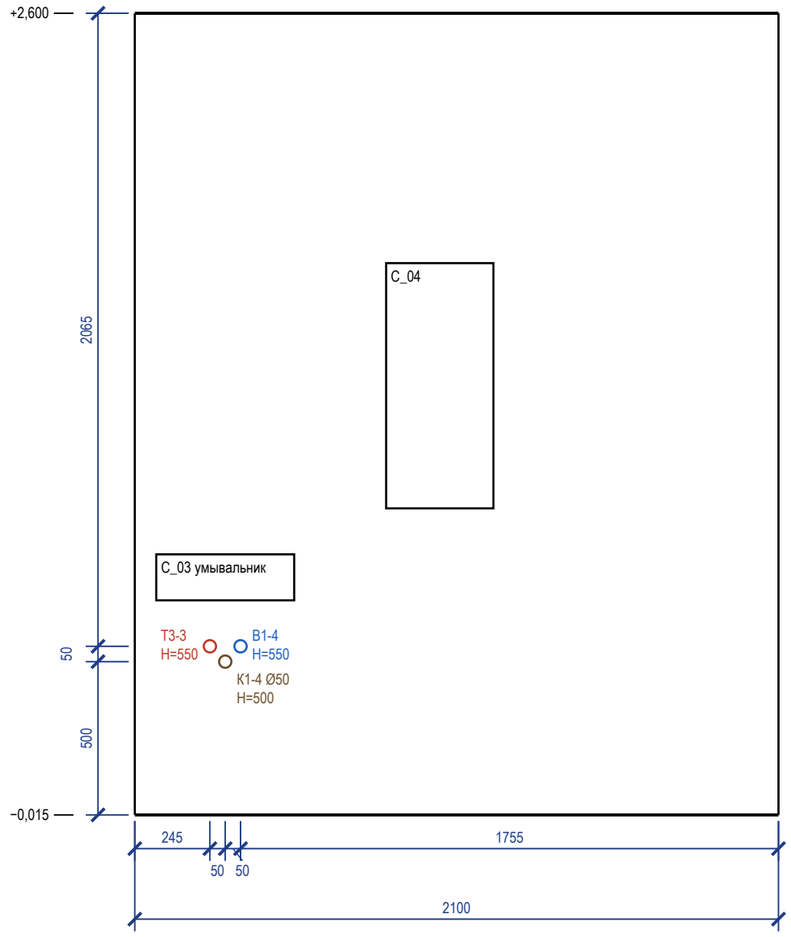

Ведомость привязок выводов (от чистого пола и угла)

Код	Прибор	Ø	H, мм	Привязка, мм
В1-3	С_02 ванна	½"	800	ст. А: 825 от лев. угла
Т3-2	С_02 ванна	½"	800	ст. А: 675 от лев. угла
К1-3	С_02 ванна	Ø50	50	ст. А: 200 от лев. угла
В1-4	С_03 умывальник	½"	550	ст. В: 345 от лев. угла
Т3-3	С_03 умывальник	½"	550	ст. В: 245 от лев. угла
К1-4	С_03 умывальник	Ø50	500	ст. В: 295 от лев. угла

Условные обозначения


- вывод В1 (код — в ведомости привязок)
- вывод Т3 (код — в ведомости привязок)
- вывод К1 (код — в ведомости привязок)
- сантехприбор по расстановке (габарит модели)
- дверной проём; окно — сплошной контур

Примечания

1. Габариты и высоты приборов, межосевые смесителей и места кранов — по паспортам выбранных приборов, сверяются до разметки стен.
2. Высоты Н — от чистого пола помещения, мм; отметка чистого пола и потолка — у левого края вида (от ±0,000 объекта). Привязки — от левого чистового угла вида (облицовка стен вычтена), как на развёртках стен.
3. Стояки в помещении: Ст К1-1 Ø110, Ст В1-1 Ø32, Ст Т3-1 Ø32 — положение на плане выводов; выводы подключаются к ним по схеме разводки.
4. Ревизионные люки к арматуре и ревизиям в данных не заданы: место и размер не определены (записи реестра нет).
5. Часть подписей выводов не уместилась у знака: коды и высоты — в ведомости привязок.
6. Помещение «Ванная» — 2 листа: стены 1) А, Б, В; 2) Г.
7. Расчёт систем водоснабжения и канализации и подбор оборудования выполняет проектная организация; лист задаёт места и высоты выводов.

					Проект: Квартира 58 м²	М 1:20
	Лист	№ док.	Подпись	Дата	Развёртки мокрых зон: выводы ВК. Ванная (лист 1 из 2)	Стадия / Лист / Листов
Дизайнер	Кырлан А.С.			04.11.26		П / 20 / 71

Стена Г (М 1:20)

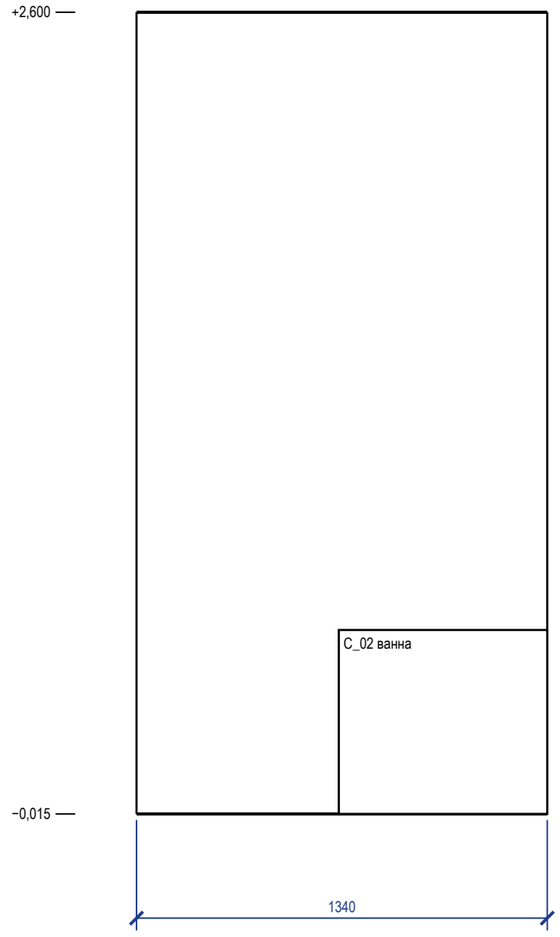

Ведомость привязок выводов (от чистого пола и угла)

Код	Прибор	Ø	H, мм	Привязка, мм
	выводов на стене нет			

Условные обозначения

- вывод В1 (код — в ведомости привязок)
- вывод Т3 (код — в ведомости привязок)
- вывод К1 (код — в ведомости привязок)
- сантехприбор по расстановке (габарит модели)
- дверной проём; окно — сплошной контур

Примечания

1. Габариты и высоты приборов, межосевые смесители и места кранов — по паспортам выбранных приборов, сверяются до разметки стен.
2. Высоты H — от чистого пола помещения, мм; отметка чистого пола и потолка — у левого края вида (от ±0,000 объекта). Привязки — от левого чистового угла вида (облицовка стен вычтена), как на развёртках стен.
3. Стояки в помещении: Ст К1-1 Ø110, Ст В1-1 Ø32, Ст Т3-1 Ø32 — положение на плане выводов; выводы подключаются к ним по схеме разводки.
4. Ревизионные люки к арматуре и ревизиям в данных не заданы: место и размер не определены (записи реестра нет).
5. Помещение «Ванная» — 2 листа: стены 1) А, Б, В; 2) Г.
6. Расчёт систем водоснабжения и канализации и подбор оборудования выполняет проектная организация; лист задаёт места и высоты выводов.

	Лист	№ док.	Подпись	Дата
Дизайнер	Кырлан А.С.			04.11.26


Проект: Квартира 58 м² — **М 1:20**

Развёртки мокрых зон: выводы ВК. Ванная (лист 2 из 2)

Стадия	Лист	Листов
П	21	71

выпуск 04.11.2026 № e0dc2f2b59 · стр. 21 из 71

Стена Г (М 1:20)

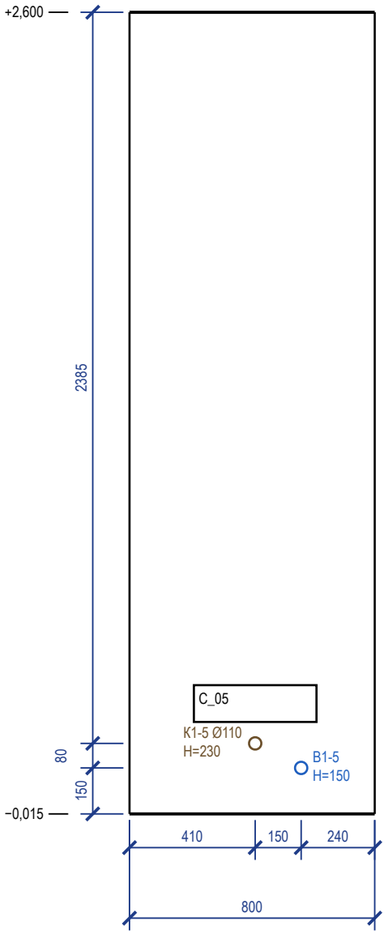

Ведомость привязок выводов (от чистого пола и угла)

Код	Прибор	Ø	H, мм	Привязка, мм
B1-5	C_05 унитаз подвесной	½"	150	ст. Г: 560 от лев. угла
K1-5	C_05 унитаз подвесной	Ø110	230	ст. Г: 410 от лев. угла

Условные обозначения

- вывод B1 (код — в ведомости привязок)
- вывод T3 (код — в ведомости привязок)
- вывод K1 (код — в ведомости привязок)
- сантехприбор по расстановке (габарит модели)
- дверной проём; окно — сплошной контур

Примечания

1. Габариты и высоты приборов, межосевые смесителей и места кранов — по паспортам выбранных приборов, сверяются до разметки стен.
2. Высоты H — от чистого пола помещения, мм; отметка чистого пола и потолка — у левого края вида (от ±0,000 объекта). Привязки — от левого чистового угла вида (облицовка стен вычтена), как на развёртках стен.
3. Ревизионные люки к арматуре и ревизиям в данных не заданы: место и размер не определены (записи реестра нет).
4. Расчёт систем водоснабжения и канализации и подбор оборудования выполняет проектная организация; лист задаёт места и высоты выводов.


					Проект: Квартира 58 м² — М 1:20
	Лист	№ док.	Подпись	Дата	
Дизайнер	Кырлан А.С.			04.11.26	Развёртки мокрых зон: выводы ВК. Санузел
					Стадия: П · Лист: 22 · Листов: 71

Поз.	Наименование и техническая характеристика	Тип, марка, обозначение документа	Код продукции	Поставщик	Ед. изм.	Кол.	Масса 1 ед., кг	Примечание
	Санитарные приборы							
1	Ванна встраиваемая акриловая 1500×700 мм, с каркасом, экраном и отверстием слив-перелив	акриловая 1500×700, смеситель настенный		выбор заказчика	шт	1		С_02
2	Унитаз подвесной безободковый, с сиденьем микролифт, крепёж и звукоизолирующая прокладка	Laufen Pro 8.2096.6.000.000.1		выбор заказчика	шт	1		С_05
3	Инсталляция для подвесного унитаза: рама высотой 1120 мм, бачок, клавиша смыва (ось клавиши 1050 мм от чистого пола)	аналог		выбор заказчика	шт	1		С_05; короб ГКЛВ
4	Умывальник подвесной 450×450 мм, с отверстием под смеситель и переливом	Laufen Pro S 8.1096.3.000.104.1		выбор заказчика	шт	1		С_03
5	Мойка кухонная 700×480 мм, с переливом	мойка врезная 700×480 в шкафу М_02		с кухонной мебелью	шт	1		С_01
6	Полотенцесушитель электрический, IP44, с терморегулятором	аналог		выбор заказчика	шт	1		С_04
	Смесители, сифоны и арматура приборов							
7	Смеситель для ванны настенный однорычажный, межосевое 150 мм, с душевым набором (лейка, шланг, держатель)	аналог		выбор заказчика	шт	1		С_02
8	Смеситель для умывальника однорычажный, с донным клапаном	аналог		выбор заказчика	шт	1		С_03
9	Смеситель кухонный однорычажный, высокий излив	аналог		выбор заказчика	шт	1		С_01
10	Обвязка ванны слив-перелив Ø40/50 с сифоном	аналог		выбор заказчика	шт	1		С_02
11	Сифон для умывальника бутылочный Ø32/40–50, с гофрой к выпуску	аналог		выбор заказчика	шт	1		С_03
12	Сифон для мойки Ø40/50	аналог		выбор заказчика	шт	1		С_01
13	Сифон для стиральной машины встраиваемый в стену Ø50, с обратным клапаном	аналог		выбор заказчика	шт	1		ОБ_02
14	Кран угловой ½"×½" с гибкой подводкой 40 см (умывальники, мойка)	аналог		выбор заказчика	шт	4		по 2 на прибор
15	Кран шаровой угловой ½"×¾" для подключения стиральной и посудомоечной машины	аналог		выбор заказчика	шт	1		ОБ_02
	Трубопроводы							
16	Труба полипропиленовая PP-R PN20 Ø20×3,4 (В1)	ГОСТ 32415-2013		выбор заказчика	м	13,5	0,17	9,2 + 2,6 + 10 %
17	Труба PP-R, армированная стекловолокном, PN20 Ø20×2,8 (Т3)	ГОСТ 32415-2013		выбор заказчика	м	9,5	0,15	6,4 + 1,9 + 10 %
18	Труба канализационная ПП Ø40 (К1)	ГОСТ 32414-2013		выбор заказчика	м	2,5		1,7 + 0,6 + 10 %
19	Труба канализационная ПП Ø50 (К1)	ГОСТ 32414-2013		выбор заказчика	м	8		6,1 + 0,9 + 10 %
20	Труба канализационная ПП Ø110 (К1)	ГОСТ 32414-2013		выбор заказчика	м	1,5		0,8 + 0,2 + 10 %
	Фасонные части и выводы							
21	Отвод канализационный ПП 45° Ø40	ГОСТ 32414-2013		выбор заказчика	шт	2		2 шт. на поворот
22	Отвод канализационный ПП 45° Ø50	ГОСТ 32414-2013		выбор заказчика	шт	12		2 шт. на поворот
23	Отвод канализационный ПП 45° Ø110	ГОСТ 32414-2013		выбор заказчика	шт	6		2 шт. на поворот
24	Тройник канализационный ПП 45° (врезки ветвей)	ГОСТ 32414-2013		выбор заказчика	шт	4		
25	Ревизия канализационная ПП (после поворота трассы)	ГОСТ 32414-2013		выбор заказчика	шт	5		доступ сохранить
26	Фитинги PP-R Ø20: тройники, угольники 90° (ветви и повороты В1, Т3)	ГОСТ 32415-2013		выбор заказчика	шт	22		
27	Водорозетка PP-R Ø20×½" настенная, с креплением	ГОСТ 32415-2013		выбор заказчика	шт	8		коды — лист выводов
	Узлы ввода, люки, короба							
28	Кран шаровой латунный Ду15 PN16 (отключение ввода)	аналог		выбор заказчика	шт	2		Ст В1-1, Ст Т3-1
29	Фильтр сетчатый косой Ду15	аналог		выбор заказчика	шт	2		
30	Счётчик воды крыльчатый Ду15 (ХВ, ГВ), с поверкой	аналог		выбор заказчика	шт	2		пломба УК
31	Клапан обратный Ду15	аналог		выбор заказчика	шт	2		
32	Люк ревизионный нажимной под плитку 300×400 мм	аналог		выбор заказчика	шт	1		к стоякам и арматуре
33	Звукоизоляция стояка К1 в коробе: рулонный звукоизоляционный материал ≥ 10 мм, обмотка стояка на высоту этажа	аналог		выбор заказчика	м	2,7		Ст К1-1
34	Короб К1 над полом: профиль ПН/ПС, ГКЛВ 12,5 мм под плитку	аналог		выбор заказчика	м	1,6		сечение — лист разводки

Примечания

1. Форма 1 ГОСТ 21.110-2013, ширины граф изменены по п. 4.1. «Аналог» — аналог по характеристикам: модели внести до черновых работ, привязки выводов сверить по паспортам.
2. Бытовая техника не входит (показана арматура подключения), мойка — в комплекте кухни (марка — модуля кухни, как у столяра). Длины труб — трасса листа разводки + подъёмы + 10 %.
3. Стояк К1 в коробе — звукоизоляция стояка в коробе без жёсткого контакта короба с трубой.
4. Расчёт систем водоснабжения и канализации, диаметры магистралей и подбор оборудования выполняет проектная организация.

					Проект: Квартира 58 м²	
	Лист	№ док.	Подпись	Дата	Спецификация сантехнического оборудования	Стадия / Лист / Листов
Дизайнер	Кырлан А.С.			04.11.26		П / 23 / 71

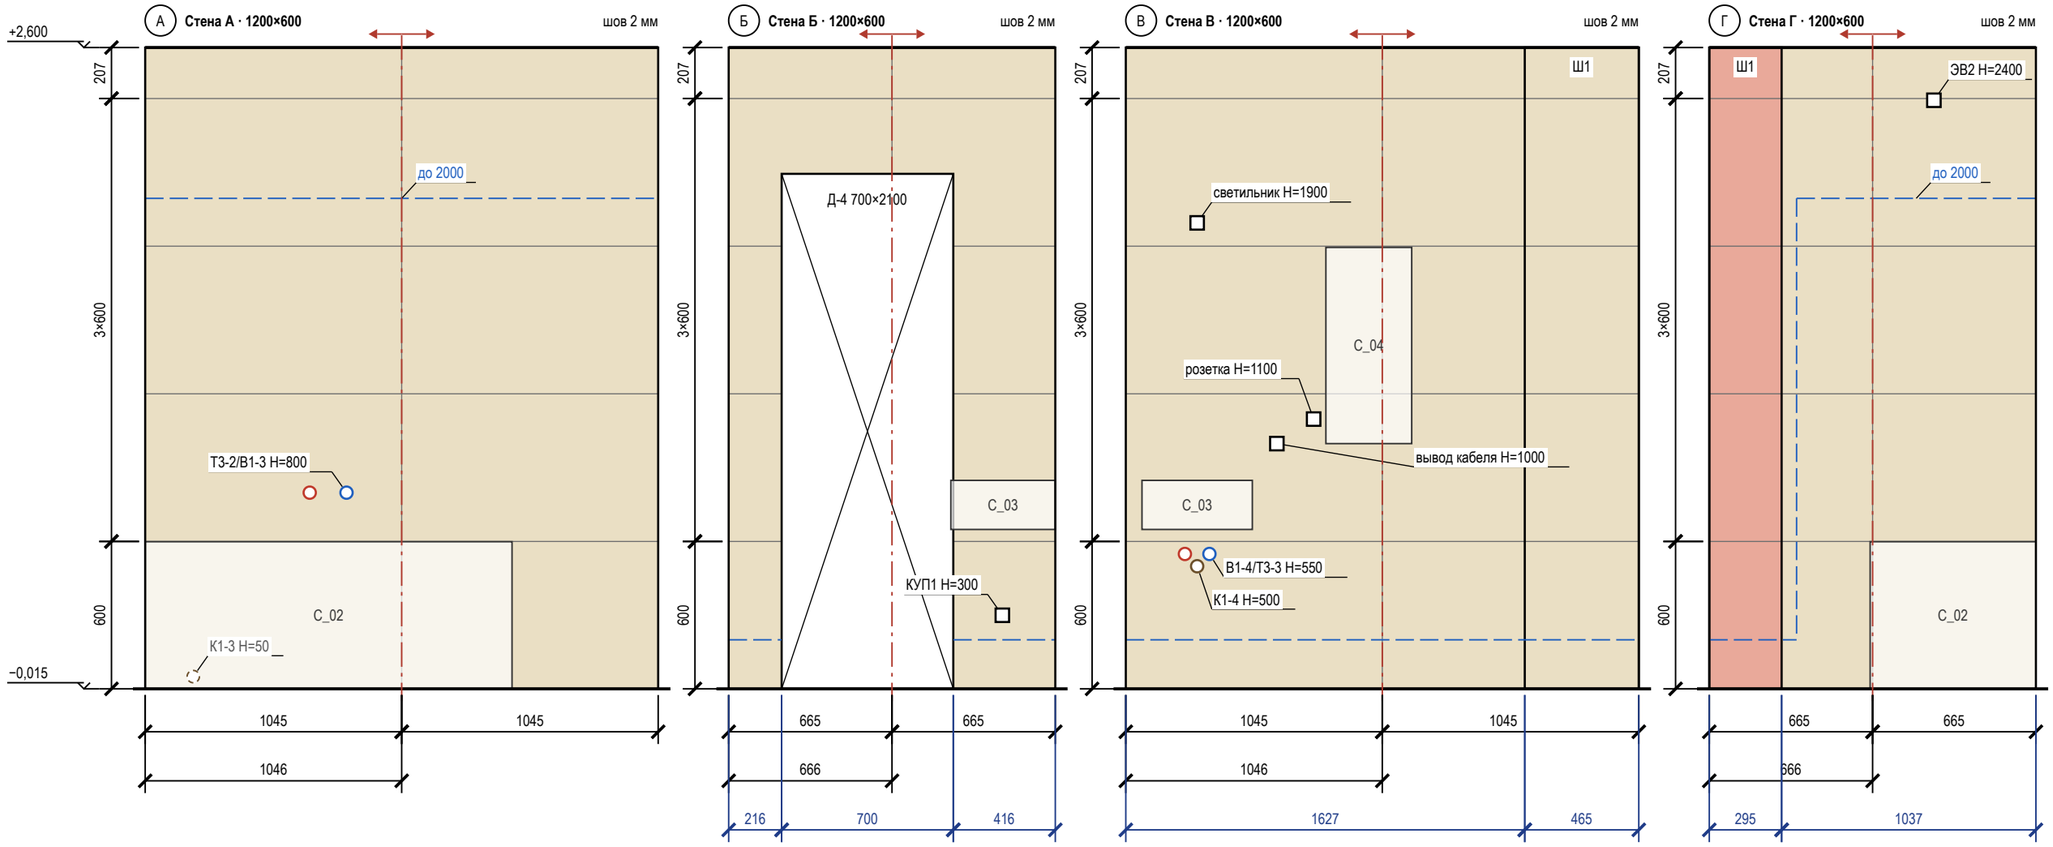

Подсчёт плитки по стенам и коробу

Поверхность	L × H, мм	S, м²	Целых	Подр.	С запасом	Подрезки: край / верх, мм
стена А	2092 × 2615	5,60	0	10	11	1045 / 1045; 207
стена Б	1332 × 2615	2,14	0	10	11	665 / 665; 207
стена В	2092 × 2615	4,38	0	10	11	1045 / 1045; 207
Ш1 489×319, ст. В	465 × 2615	1,22	0	5	6	лицо 465
стена Г	1332 × 2615	2,84	0	10	11	665 / 665; 207
Ш1 489×319, ст. Г	295 × 2615	0,77	0	5	6	лицо 295
Итого		**16,94**	**0**	**50**	**56**	

Сдвиг точек под раскладку

Точка (ВК, ЭОМ)	Стена	Проект: от угла / Н	Под раскладку: от угла / Н	Сдвиг, мм
розетка	В	766 / 1100	766 / 1203	Н +103
вывод кабеля	В	616 / 1000	616 / 902	Н −98
светильник	В	291 / 1900	291 / 1805	Н −95

Примечания

1. Вид изнутри, стены по часовой стрелке А → Г. Высоты — от чистого пола (−0,015), отметки — от ±0,000. Раскладка от чистовых размеров (штукатурка 10 + клей 5 + плитка 9 мм), подрезки чистые; старт — от оси стены, ряды от пола целыми.
2. Облицовка до потолка (+2,600).
3. Точки из таблицы сдвигов переносятся до черновой разводки (ЭОМ — по тем же числам).
4. Выводы ВК стоят по оси прибора и с прибором не двигаются — привязки по «Плану выводов сантехники» без сдвига; вне сетки (Т3-2/В1-3, В1-4/Т3-3, К1-4) отверстие в плитке коронкой по той же привязке, плитку не сдвигать.
5. За приборами и в коробе (К1-3) — штриховым кольцом.
6. Гидроизоляция: 200 мм от ЧП по периметру; над ванной — до 2000 и 300 мм за борт (СП 29.13330.2011, п. 7.2 — на высоту замачивания); углы — лентой; акт скрытых работ, пролив.
7. Короб стояков Ш1: грани 465 мм (ст. В), 295 мм (ст. Г) — плиткой стен по рядам стены, целая плитка от наружного угла; угол — запил 45° или профиль; за коробом плитку не кладут. Люк 300×400 — на грани ст. В: высота — по месту ревизии стояка (положение стояков сверяется на объекте), кромки дверцы по швам сетки, дверца нажимная под плитку.

Условные обозначения


- плитка целая; тонкая линия — шов
- плитка с подрезкой (размер — на цепочке)
- ось старта; стрелки — направление укладки
- верх гидроизоляции: 200 от ЧП, в мокрой зоне — «до …»
- проём — не облицовывается
- сантехприбор: габарит, высота по практике
- грань короба стояков (Ш…): своя сетка, за коробом плитку не кладут
- вывод В1 (код — в ведомости привязок)
- вывод Т3 (код — в ведомости привязок)
- вывод К1 (код — в ведомости привязок)
- вывод за прибором / в коробе (не на сетке)
- электроточка: марка и Н — по листам ЭОМ
- отметка уровня, м: ±0,000 — чистый пол жилых помещений
- низ потолка; серая полоса — стена без плитки
- (А) обозначение стены А–Г (как на развёртках)

	Лист	№ док.	Подпись	Дата
Дизайнер	Кырлан А.С.			04.11.26

Проект: Квартира 58 м² — **М 1:25**

Раскладка плитки. Ванная. Развёртки стен

Стадия	Лист	Листов
П	24	71

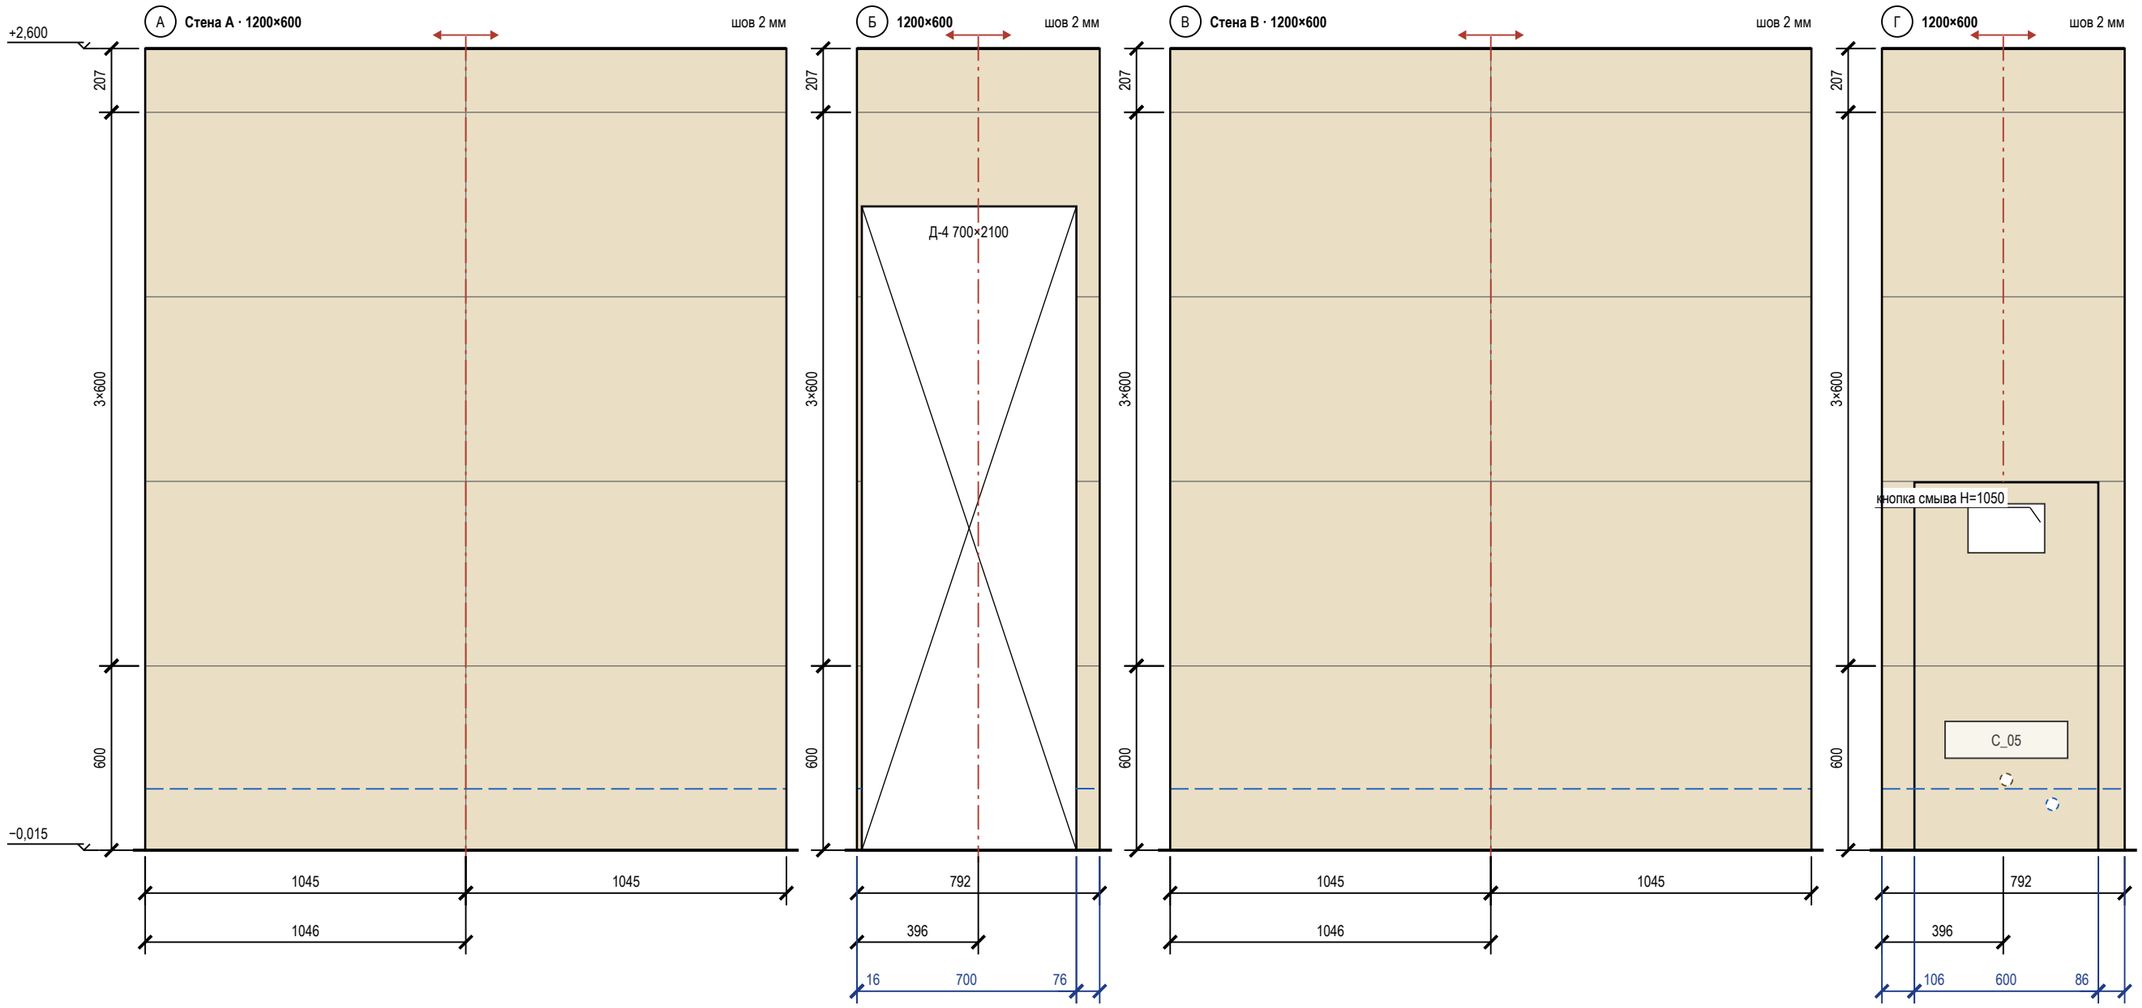

Подсчёт плитки по стенам и коробу

Поверхность	L × H, мм	S, м²	Целых	Подр.	С запасом	Подрезки: край / верх, мм
стена А	2092 × 2615	5,60	0	10	11	1045 / 1045; 207
стена Б	792 × 2615	0,73	0	5	6	792; 207
стена В	2092 × 2615	5,60	0	10	11	1045 / 1045; 207
стена Г	792 × 2615	1,48	0	5	6	792; 207
короб (ст. Г)	600×1200×250	1,47	0	7	8	лицо 600; бок. 250
Итого		**14,87**	**0**	**37**	**42**	

Условные обозначения

- плитка целая; тонкая линия — шов
- плитка с подрезкой (размер — на цепочке)
- ось старта; стрелки — направление укладки
- верх гидроизоляции: 200 от ЧП, в мокрой зоне — «до …»
- проём — не облицовывается
- сантехприбор: габарит, высота по практике
- короб инсталляции, в нём кнопка смыва 250×160
- вывод В1 (код — в ведомости привязок)
- вывод К1 (код — в ведомости привязок)
- вывод за прибором / в коробе (не на сетке)
- отметка уровня, м: ±0,000 — чистый пол жилых помещений
- низ потолка; серая полоса — стена без плитки
- (А) обозначение стены А–Г (как на развёртках)

Примечания


1. Вид изнутри, стены по часовой стрелке А → Г. Высоты — от чистого пола (−0,015), отметки — от ±0,000. Раскладка от чистовых размеров (штукатурка 10 + клей 5 + плитка 9 мм), подрезки чистые; старт — от оси стены, ряды от пола целыми.
2. Облицовка до потолка (+2,600).
3. Открытые выводы и электроточки — на шве или в центре плитки (допуск 10 мм; плитка от 900 мм по высоте — на шве или не ближе 60 мм к нему).
4. За приборами и в коробе (В1-5, К1-5) — штриховым кольцом.
5. Гидроизоляция: 200 мм от ЧП по периметру; углы — лентой; акт скрытых работ, пролив.
6. Короб 600×1200×250: лицо 600 мм от оси кнопки смыва, боковины, полка; углы — запил 45° или профиль; за коробом плитку не кладут.
7. Между коробом и углом полоса 86 и 106 мм — довести короб до угла.

	Лист	№ док.	Подпись	Дата
Дизайнер	Кырлан А.С.			04.11.26

Проект: Квартира 58 м² — **М 1:20**

Раскладка плитки. Санузел. Развёртки стен

Стадия	Лист	Листов
П	25	71

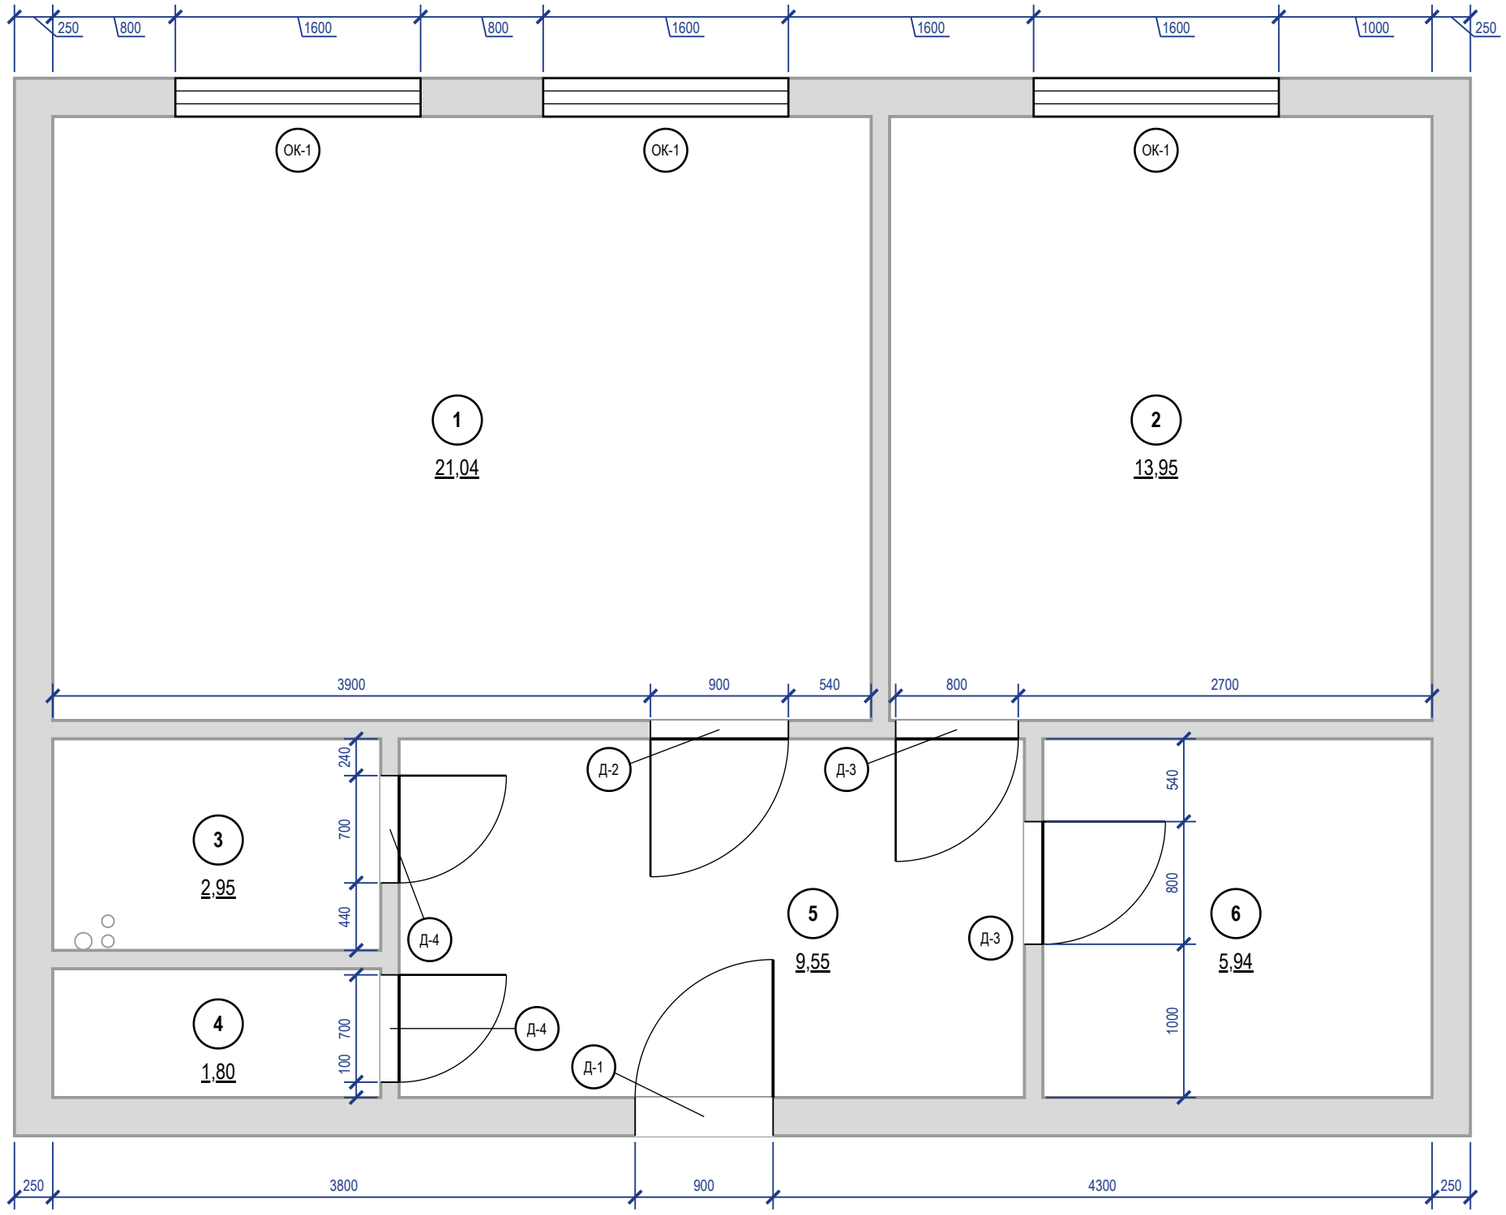

Примечания

1. Размеры проёмов и привязки — в миллиметрах от чистых граней стен до отделки; привязка — от угла того помещения, со стороны которого стоит размер. Размер проёма — ширина × высота от чистого пола 0,000. Размеры на плане — проёмов, не полотен: полотно — в ведомости, коробка — по системе. Откос от угла помещения до проёма с коробкой — не менее 50 мм.
2. Марки в кружках — типы заполнения проёмов (ГОСТ 21.501-2018, п. 5.3.2); одна марка — один типоразмер; количество сверено с планом.
3. Д-2…Д-4 — существующие проёмы, до техзаключения не расширять.
4. Экспликация помещений — лист 5; в марках помещений — номер и площадь, м².
5. Ведомость заполнения проёмов, открывание полотен, заказ и порядок монтажа блоков — лист 27.
6. Привязка проёма к углу помещения меньше 1 мм на листе, размер на плане не показан: Д-3 — 40 мм; Д-4 — 40 мм.

					Проект: Квартира 58 м²	М 1:40
	Лист	№ док.	Подпись	Дата	План размещения дверей	Стадия / Лист / Листов
Дизайнер	Кырлан А.С.			04.11.26		П / 26 / 71

выпуск 04.11.2026 № e0dc2f2b59 · стр. 26 из 71


Ведомость заполнения проёмов

Марка	Наименование, обозначение	Проём ш×в, мм	Полотно (расч.)	Кол.	Откр.	Отделка полотна	Фурнитура	Прим.
Д-1	Блок дверной входной, ГОСТ 31173-2016	900×2100	блок задать	1	Л	в комплекте блока	в комплекте блока (замки, глазок)	
Д-2	Дверь скрытого монтажа, Софья (SOFIA) Скрытые двери	900×2100	800×2000	1	Л	S 1502-Y50R — пом. 5, S 1002-Y50R — пом. 1	скрытые петли 3D, магнитный замок	
Д-3	Дверь скрытого монтажа, Софья (SOFIA) Скрытые двери	800×2100	700×2000	2	Л, П	окраска S 1502-Y50R с двух сторон; V503 пом. 6, S 1502-Y50R пом. 5	скрытые петли 3D, магнитный замок	
Д-4	Дверь скрытого монтажа, Софья (SOFIA) Скрытые двери	700×2100	600×2000	2	П, П	S 1502-Y50R — пом. 5, в тон облицовки — пом. 3; S 1502-Y50R — пом. 5, в тон облицовки пом. 4	скрытые петли 3D, магнитный замок, фиксатор WC	порог 15
ОК-1	Блок оконный, ГОСТ 23166-2021	1600×1600		3				низ 800

Примечания

1. Марки проёмов — те же, что на плане размещения дверей (лист 26); привязки проёмов — там же.
2. Открывание: Л — петли слева, П — справа, если смотреть со стороны, куда открывается полотно (на себя).
3. Скрытые двери (Д-2…Д-4): проём замерить в чистоте; блок заказать до штукатурки (≈ 30 дн.), короб ставить до штукатурки; полотно навесить после чистовой отделки, красить в цвет стен. Порядок — практика монтажа, изготовитель подтверждает.
4. Полотно «расч.» — по проёму с запасом по каталогам, заказ — по таблице проёмов модели; Д-2…Д-4: проём 2100, а под полотно 2000 по каталогам нужен 2050–2080, под 2100 2150–2180: высоту проёма — по модели; Д-1: входной блок по ГОСТ 31173-2016 — задать при выборе блока.


Схемы дверных блоков (1:25) — вид со стороны открывания; вершина треугольника — сторона петель

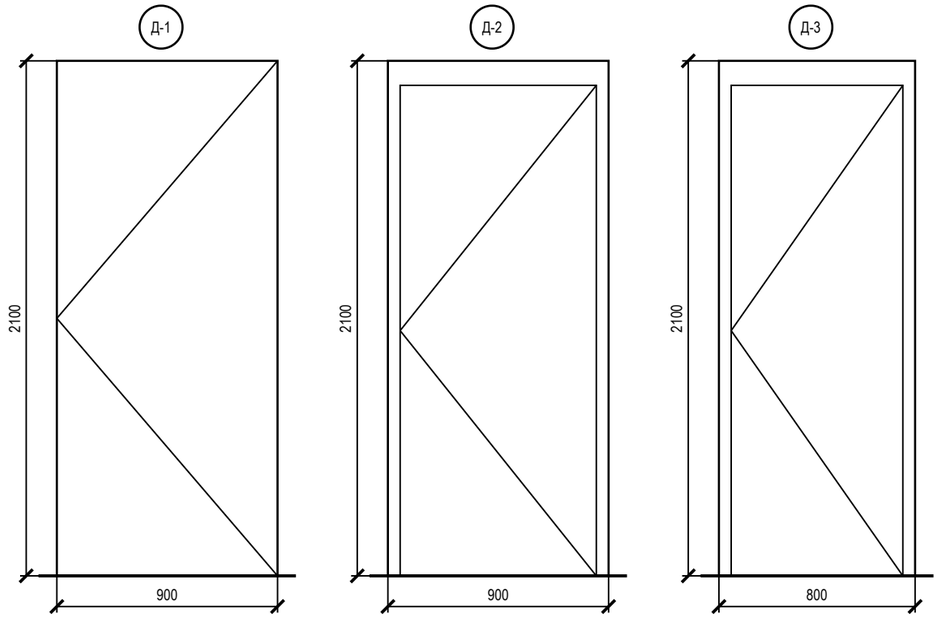

блок — по ГОСТ 31173
откр. Л


полотно 800×2000 (расч.)
откр. Л

полотно 700×2000 (расч.)
откр. Л, П (схема — Л, остальные по плану)

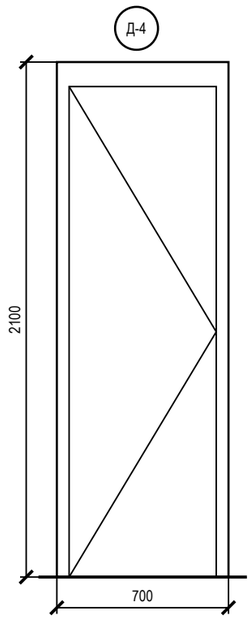

полотно 600×2000 (расч.)
откр. П, П

					Проект: Квартира 58 м²	
	Лист	№ док.	Подпись	Дата	Ведомость заполнения проёмов	Стадия / Лист / Листов
Дизайнер	Кырлан А.С.			04.11.26		П / 27 / 71

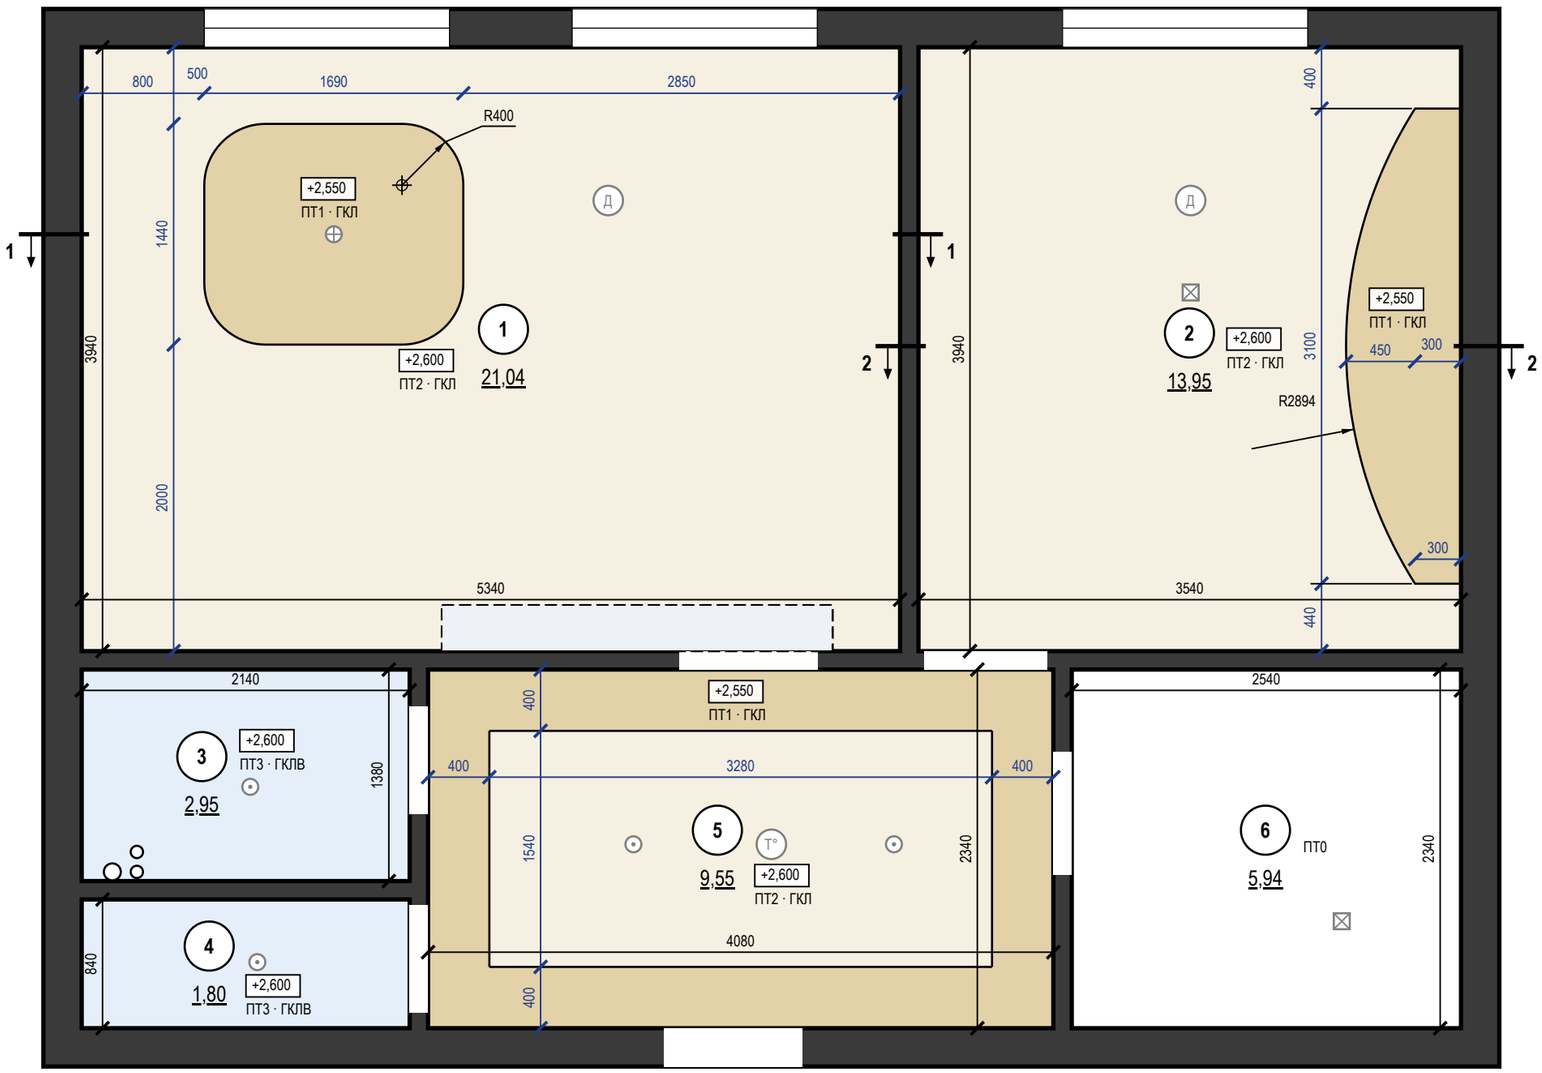

Ведомость потолков

Пом.	Марка	Конструкция	Низ / верх ниши	S, м²	Q
1	ПТ1	ГКЛ П113, остров	+2,550	2,30	Q3
1	ПТ2	ГКЛ П113	+2,600	18,74	Q3
2	ПТ1	ГКЛ П113, дуга	+2,550	1,88	Q3
2	ПТ2	ГКЛ П113	+2,600	12,07	Q3
3	ПТ3	ГКЛВ П113	+2,600	2,95	Q3
4	ПТ3	То же	+2,600	1,80	Q3
5	ПТ1	ГКЛ П113	+2,550	4,50	Q3
5	ПТ2	ГКЛ П113	+2,600	5,05	Q3
6	ПТ0	Существующий потолок, окраска	+2,700	5,94	
		Итого		**55,23**	

Ведомость вырезов и закладных в потолке

Марка	Устройство	Кол.	Пом.
	Светильник встраиваемый (марки — план освещения)	4	3, 4, 5
	Светильник накладной (марки — план освещения)	2	2, 6
	Светильник подвесной (марки — план освещения)	1	1
	Извещатель дымовой	2	1, 2
	Извещатель тепловой	1	5

Примечания


1. За отметку ±0,000 принят уровень чистого пола сухих помещений (готовое покрытие), а не существующего пола; пол пом. 3, 4 — −0,015; верх плиты перекрытия −0,064 — расчётный по пирогу пола, не замерен; существующий пол снимается до плиты, его отметка не замерена. Отметки в прямоугольниках — низ потолка; низ перекрытия +2,700. Марка потолка — одна конструкция и отметка на весь альбом.
2. Размеры помещений в свету (ширина × длина, мм), не поместившиеся на плане: пом. 4 — 2140 × 840.
3. Потолки ГКЛ — каркасная система П113: подвесы через 1000 (с запасом: СП 163, табл. 14 — до 1100 при 0,15 кН/м²), несущие профили через 500, основные через 1200 мм; листы — поперёк несущих профилей. В помещениях 3, 4 — ГКЛВ на оцинкованном каркасе.
4. Нижний уровень — пояс-короб по периметру шириной 400 мм, верхний — поле внутри пояса: пом. 5.
5. Примыкание к стенам: теневой шов 15 мм, техзазор 3 мм — пом. 1, 2, 5, по стенам, выровненным штукатуркой (узел 1); пом. 3, 4 — разделительная лента.
6. Светильники и потолочные устройства — подложка с планов освещения, слаботочных систем и вентиляции (положение — по ним); вырезы и закладные — по ведомости на листе, до обшивки; отверстия не совмещать с профилями, глубина корпуса светильника до 70 мм.
7. Разрезы 1–1, 2–2 — на листе 29; высоты мебели и дверных блоков сверены с низом потолка в разрезах; гибка бортов фигур и ленты ниш — там же; размеры фигурных уровней — фрагменты 1, 2 (лист 30).
8. Шпаклевание ГКЛ и условия приёмки — Q3: рассеянный дневной свет, осмотр с 2 м; боковой свет не оценивается.
9. Пом. 1: короб воздуховода кухонной вытяжки ГКЛ 300×200 мм (ширина от стены × высота), низ +2,500, длина 2,25 м — по трассе плана вентиляции, вдоль стен до входа в канал под воздуховод Ø125; каркас ПН 28×27 по стене и плите, ПП 60×27, лист ГКЛ 12,5.
10. ПТ0 — пом. 6: существующий потолок, окраска, без подвесного потолка, низ +2,700; материал и цвет — по ведомости отделки.

					Проект: Квартира 58 м² — **М 1:40**
	Лист	№ док.	Подпись	Дата	План потолков — Стадия: П; Лист: 28; Листов: 71
Дизайнер	Кырлан А.С.			04.11.26	

выпуск 04.11.2026 № e0dc2f2b59 · стр. 28 из 71


Разрез 1–1 (М 1:40)

Пом. 1 Кухня-гостиная; линия разреза — план потолков, лист 28

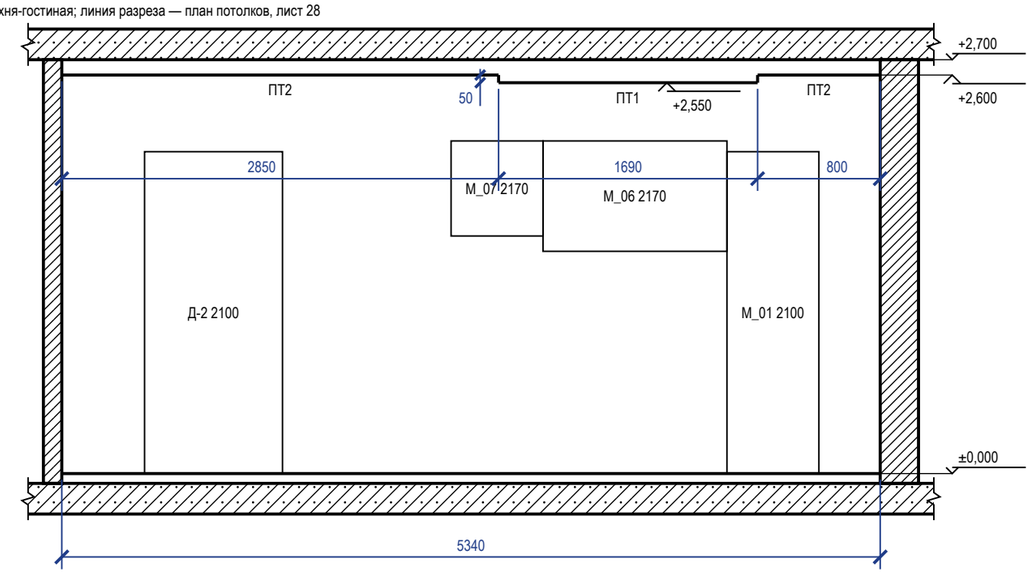

Разрез 2–2 (М 1:40)

Пом. 2 Спальня; линия разреза — план потолков, лист 28

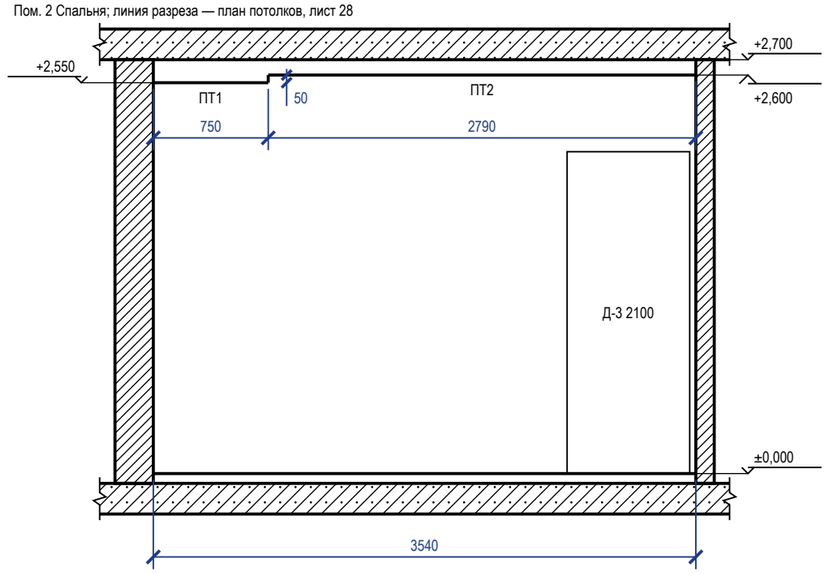

Условные обозначения

- плита перекрытия в сечении
- стена в сечении
- потолок ГКЛ в сечении; под линией — марка потолка (план потолков)
- мебель и дверные проёмы за секущей плоскостью; число — марка и верх от чистого пола, мм


Примечания

1. Разрезы — по линиям 1–1, 2–2 на плане потолков (лист 28). Отметки — от ±0,000 чистого пола, м; размеры — мм.
2. Высоты мебели и дверных блоков за секущей плоскостью сверены с низом потолка над ними: верх ниже низа короба и поля.
3. ГКЛ 12,5 мм по каркасу П113.
4. Толщины плит перекрытия и пирога пола показаны условно.
5. Ведомость объёмов потолков (лист ГКЛ, профиль, подвесы, лента, блоки питания, люки) — на листе 30.
6. Фрагменты 1, 2 — помещения с фигурными уровнями (размеры фигур, радиусы, отметки) — на листе 30.

					Проект: Квартира 58 м²	М 1:40
	Лист	№ док.	Подпись	Дата		
Дизайнер	Кырлан А.С.			04.11.26	Разрезы и узлы потолков	Стадия: П; Лист: 29; Листов: 71

Фрагмент 1. Пом. 1 Кухня-гостиная — уровни потолка (М 1:50)

Цепочки — от чистых граней стен; отметки — низ уровня от ±0,000

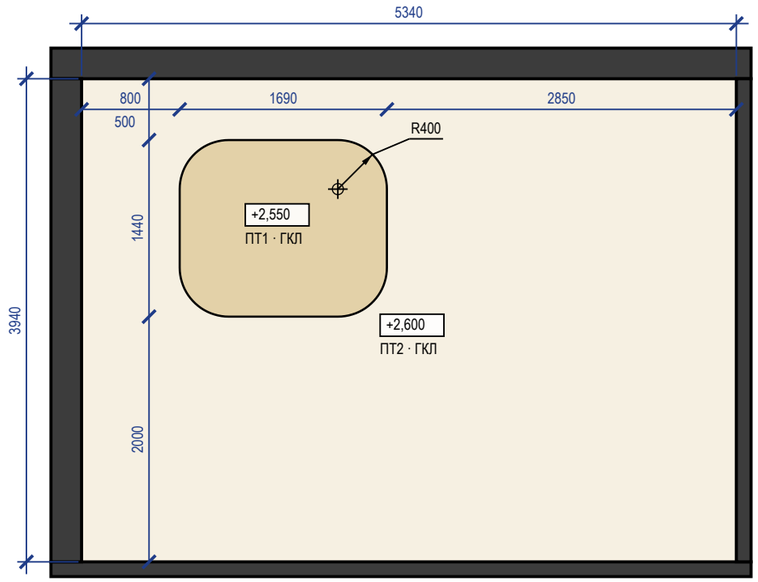


ПТ1 — низ +2,550

ПТ2 — низ +2,600

Фрагмент 2. Пом. 2 Спальня — уровни потолка (М 1:50)

Цепочки — от чистых граней стен; отметки — низ уровня от ±0,000

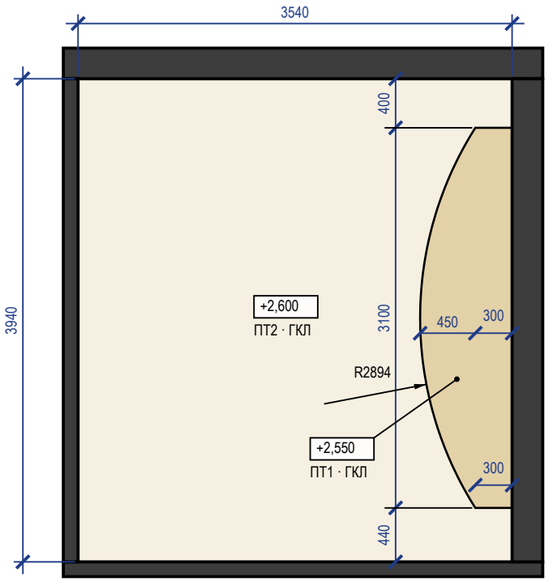

ПТ1 — низ +2,550

ПТ2 — низ +2,600

Ведомость объёмов потолков


Позиция	Ед.	Кол.	Пом.
Лист ГКЛ 12,5	м²	45,36	1, 2, 5
Лист ГКЛВ 12,5	м²	4,75	3, 4
Лист ГКЛ арочный 6,5	м²	0,25	1
Борта и карнизы (входят в площади листов выше)	м²	0,95	1, 2, 5
Профиль ПП 60×27	м	142,49	1, 2, 3, 4, 5
Профиль ПН 28×27	м	97,53	1, 2, 3, 4, 5
Подвес прямой	шт.	55	1, 2, 3, 4, 5
Анкер-клин к плите	шт.	55	1, 2, 3, 4, 5
Шуруп TN 3,5×25	шт.	1156	1, 2, 3, 4, 5
Лента армирующая для швов	м	60,29	1, 2, 3, 4, 5
Шпаклёвка для швов	кг	20,10	1, 2, 3, 4, 5
Грунтовка (швы)	л	5,02	1, 2, 3, 4, 5
Лента разделительная по периметру	м	59,36	1, 2, 3, 4, 5
Сплошная шпаклёвка и окраска (площадь развёртки)	м²	50,24	1, 2, 3, 4, 5

Примечания

1. ГКЛ 12,5 мм по каркасу П113; условные обозначения разрезов — на листе 29.
2. Фрагменты 1, 2 (план потолков — лист 28) — фигурные уровни потолка крупно: привязки краёв и центров фигур к чистым граням стен, радиусы (R) с центрами, хорда и стрелка дуги, отметки низа каждого уровня; цвета уровней — как на плане потолков.
3. Фигурные уровни: борт — ГКЛ по ПН с надрезами (на дуге шаг стоек борта 300 мм при R до 2500, 400 — до 5000) или по гнутому заводскому профилю (СП 163, 6.3.3); гибка: остров пом. 1 R400 — ГКЛ 6,5 мокрой гибкой; дуга пом. 2 R2894 — ГКЛ 12,5 сухой гибкой (СП 163, табл. 9).
4. Ведомость объёмов — по геометрии плана потолков: Лист ГКЛ 12,5 — плоскости уровней + борта (без арочных участков); Лист ГКЛВ 12,5 — плоскости уровней + борта; Лист ГКЛ арочный 6,5 — кривая борта × высота борта и стенки ниши × 2 слоя (R400 мокрая гибка); Борта и карнизы — длина перепада × перепад; Профиль ПП 60×27 — S × (1/шаг несущ. + 1/шаг осн.) + стойки бортов; Профиль ПН 28×27 — периметр стен + 2 × перепады + карнизы; Подвес прямой — по раскладке: S уровня / (шаг осн. × шаг подвесов), пояс уже шага — ряд вдоль пояса, фигура — по контуру; шаг подвесов — не больше табл. 14 СП 163; Анкер-клин к плите — по одному на подвес (Knauf П113); Шуруп TN 3,5×25 — 23 шт./м² (Knauf П113, табл. 2 альбома П 11); Лента армирующая для швов — 1,2 м/м² листа (Knauf); Шпаклёвка для швов — 0,4 кг/м² листа, только швы (Knauf); Грунтовка (швы) — 0,1 л/м² листа, только швы (Knauf); Лента разделительная по периметру — периметр стен под потолком ГКЛ; Сплошная шпаклёвка и окраска (площадь развёртки) — плоскости + борта; расход — по паспорту материала (норма расхода на сплошной слой не подтверждена); без запаса на подрезку (при закупке листа: ×1,075 при S > 20 м², ×1,175 — 10–20 м², ×1,275 — < 10 м²).

					Проект: Квартира 58 м² — М 1:50
	Лист	№ док.	Подпись	Дата	
Дизайнер	Кырлан А.С.			04.11.26	Разрезы и узлы потолков (продолжение)

Стадия	Лист	Листов
П	30	71

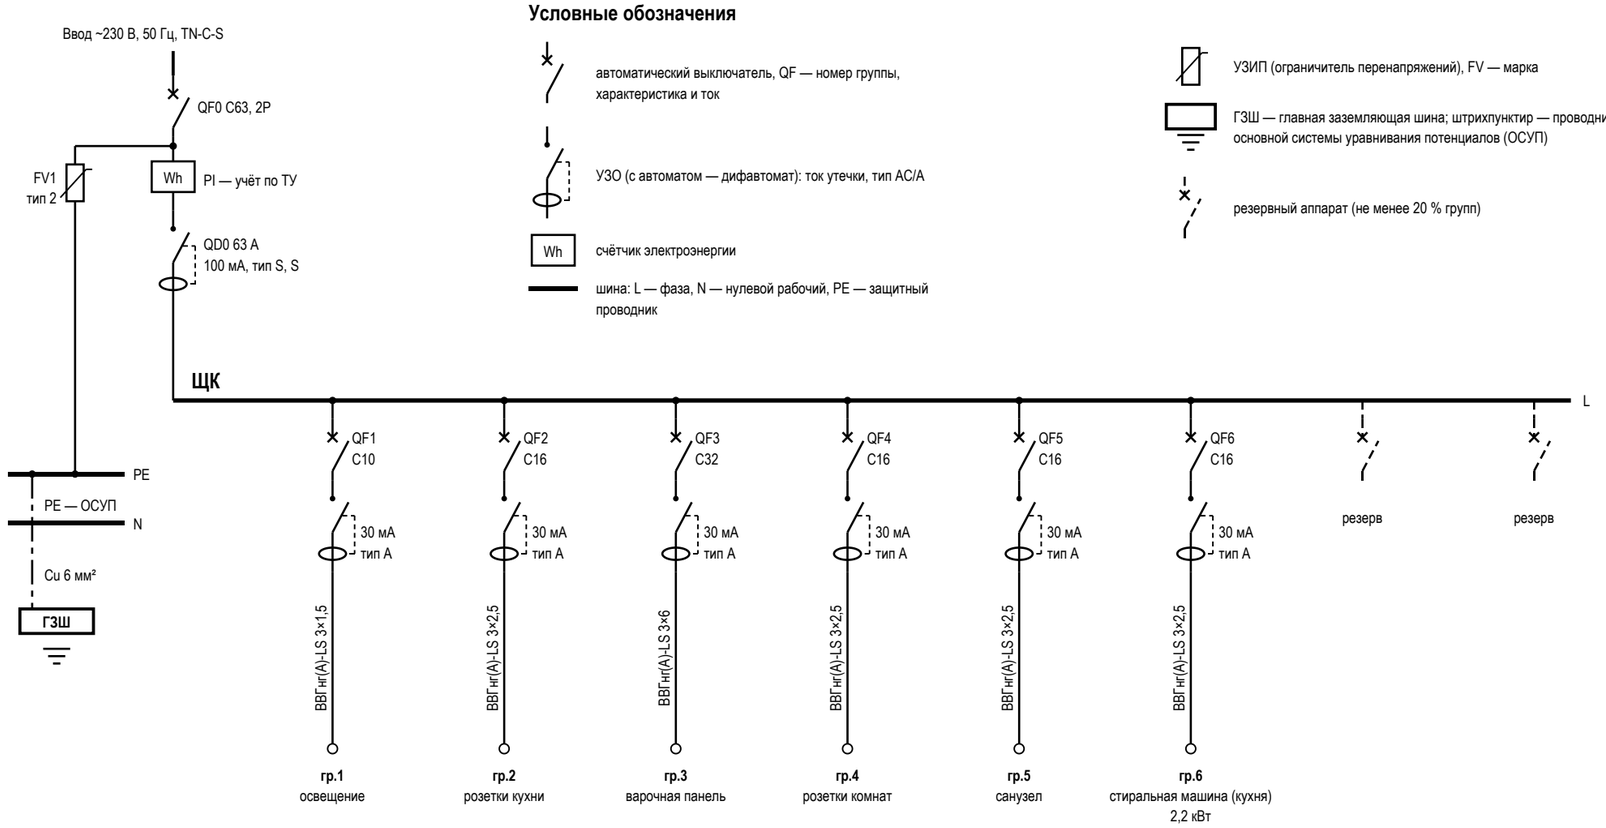

Условные обозначения

автоматический выключатель, QF — номер группы, характеристика и ток

УЗО (с автоматом — дифавтомат): ток утечки, тип AC/A

Wh — счётчик электроэнергии

шина: L — фаза, N — нулевой рабочий, PE — защитный проводник

УЗИП (ограничитель перенапряжений), FV — марка

ГЗШ — главная заземляющая шина; штрихпунктир — проводник основной системы уравнивания потенциалов (ОСУП)

резервный аппарат (не менее 20 % групп)

Данные щитка

Показатель	Значение
Номер щитка	ЩК
Тип	ЩРВ-П-24, IP41
Уст. мощность, кВт	
Разреш. мощность, кВт	15
Расчётная, кВт	9,8
Автоматы 1п: занят. / рез.	6 / 2
Модулей: всего / занято	24 / 19
Ток на вводе, А	63
Вводной аппарат	QF0 C63, 2P
УЗИП	FV1, тип 2, ЩК, после счётчика
ГЗШ, проводник ОСУП	Cu 6 мм²

Таблица групп щита ЩК и кабельный журнал


№	Назначение	Помещения	Автомат	УЗО / дифавтомат	Кабель	Длина, м	Р, кВт	Точек
1	освещение	1, 2, 3, 4, 5, 6	C10	30 мА, тип A	ВВГнг(A)-LS 3×1,5	105,4		25
2	розетки кухни	1	C16	30 мА, тип A	ВВГнг(A)-LS 3×2,5	20,8		4
3	варочная панель	1	C32	30 мА, тип A	ВВГнг(A)-LS 3×6	10,7		1
4	розетки комнат	1, 2, 5	C16	30 мА, тип A	ВВГнг(A)-LS 3×2,5	48,1		11
5	санузел	3	C16	30 мА, тип A	ВВГнг(A)-LS 3×2,5	12		2
6	стиральная машина (кухня)	1	C16	30 мА, тип A	ВВГнг(A)-LS 3×2,5	11	2,2	1
	Итого по сечениям ВВГнг(A)-LS, м: 3×1,5 — 105,4; 3×2,5 — 91,9; 3×6 — 10,7					208		

Примечания

1. Схема однолинейная: одна линия — фаза, N и PE группы; аппараты — в отключённом положении (ГОСТ 2.702, ГОСТ 2.755). Номера групп — как у точек на планах (гр.). За отметку 0,000 принят уровень чистого пола; высота щита — по плану розеток.
2. Розеточные и мокрые линии — через УЗО или дифавтомат с током утечки не более 30 мА (ПУЭ 7.1.79); в санузле выполнить ДСУП (ПУЭ 7.1.87–7.1.88).
3. УЗО тип A — для линий с электроникой, стиральной и посудомоечной машиной, LED-драйверами; тип AC — только для чисто активной нагрузки.
4. Кабель — медный, исполнение нг(A)-LS (ГОСТ 31565-2012); скрытая прокладка только горизонтально и вертикально, фактические трассы зафиксировать исполнительной схемой до закрытия отделкой.
5. Номинал автомата — не выше допустимого тока кабеля: 1,5 мм² — до 10 А, 2,5 мм² — до 16 А. Резерв щита — не менее 20 % модулей.
6. Расчёт нагрузок, токов КЗ, селективности и сечений — по проекту ЭОМ организации с допуском СРО; лист задаёт состав, расположение и группы.
7. УЗИП FV1 — после вводного автомата, проводник к шине PE — кратчайший, без петель. Шина PE щита соединяется с ГЗШ проводником ОСУП; к ГЗШ присоединяются трубы водопровода и отопления на вводе в квартиру (ПУЭ 7.1.87). Шины N и PE — раздельные, после разделения PEN не объединяются.
8. До подключения нагрузки — приёмо-сдаточные испытания с протоколом: сопротивление изоляции линий не менее 0,5 МОм, срабатывание УЗО по току и времени, непрерывность защитных проводников PE (ПУЭ, гл. 1.8).

					Проект: Квартира 58 м²
	Лист	№ док.	Подпись	Дата	Однолинейная схема щита
Дизайнер	Кырлан А.С.			04.11.26	

Стадия	Лист	Листов
П	31	71

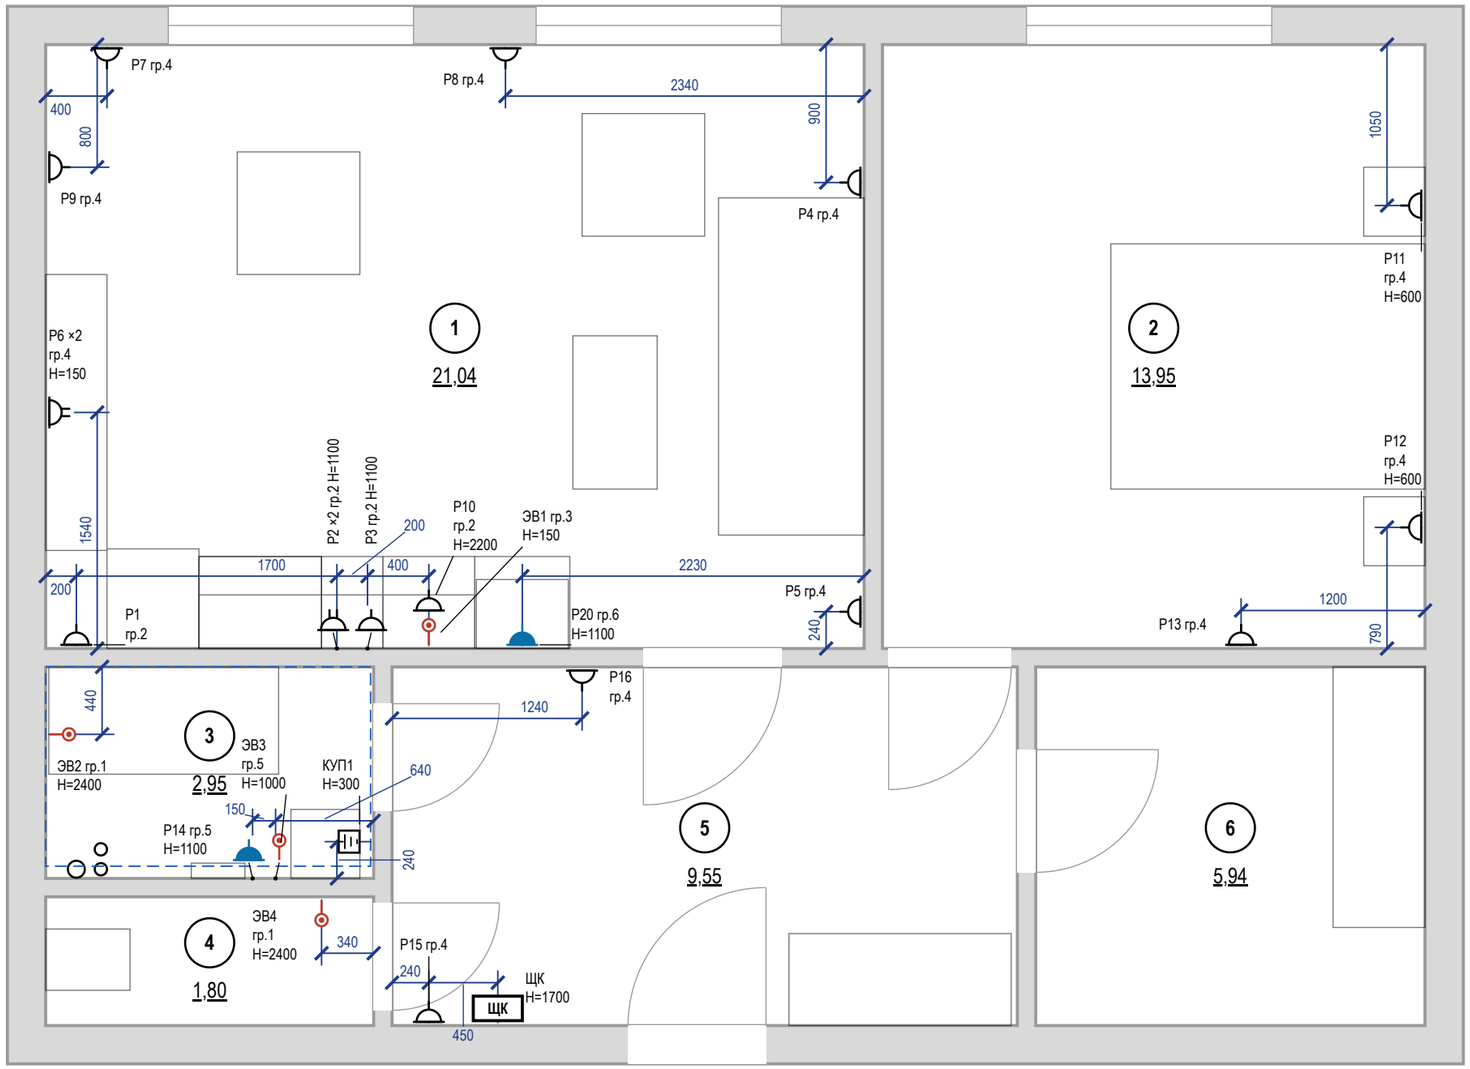

Условные обозначения

Знак	Тип изделия	Н, мм	Кол., шт
	Розетка с заземлением	300	9
	То же	у знака	4
	Блок розеток с заземлением, рамка 2 поста	у знака	2
	Розетка с заземлением IP44	1100	2
	Вывод кабеля к прибору	у знака	4
	КУП (уравнивание потенциалов)	300	1
ЩК	Щит квартирный	1700	1

розетка с заземляющим контактом; у знака — марка, ×N — постов в рамке, гр. — группа щита, Н — высота оси, мм

знак разведён для читаемости: точка на стене — у выноски, привязка — до неё

граница зоны 2 ванной (600 мм от ванны/поддона)

мебель и сантехприборы — подложка

стояк: К1 — канализация, В1 — ХВС, Т3 — ГВС

1 — номер помещения, площадь м²

Итого розеток (механизмов) — 19 шт; рамок — 17 шт: на 1 пост — 15, на 2 поста — 2.


Примечания

1. За отметку 0,000 принят уровень чистого пола. Высоты Н — от чистого пола до оси изделия; привязки — от чистовой грани стены до оси механизма (у рамки на несколько постов — до оси рамки).
2. Розетки без отметки Н у знака — на высоте 300 мм от чистого пола до оси механизма; выводы кабеля — по паспорту прибора.
3. Розетки в санузле — только вне зон 0–2 (ПУЭ 7.1.48, ГОСТ Р 50571.7.701-2024), IP44, через УЗО 30 мА.
4. Розеточные и мокрые линии — через УЗО или дифавтомат с током утечки не более 30 мА (ПУЭ 7.1.79); в санузле выполнить ДСУП (ПУЭ 7.1.87–7.1.88).
5. Кабель — медный, исполнение нг(А)-LS (ГОСТ 31565-2012); скрытая прокладка только горизонтально и вертикально, фактические трассы зафиксировать исполнительной схемой до закрытия отделкой.
6. Расчёт нагрузок, токов КЗ, селективности и сечений — по проекту ЭОМ организации с допуском СРО; лист задаёт состав, расположение и группы.
7. Выводы кухонной техники — после утверждения проекта кухни (ориентировочно); привязки выводов даны от осей модулей гарнитура и пересматриваются вместе с проектом кухни.

					Проект: Квартира 58 м² — М 1:40
	Лист	№ док.	Подпись	Дата	План розеток и электровыводов
Дизайнер	Кырлан А.С.			04.11.26	Стадия: П; Лист: 32; Листов: 71

Условные обозначения

- ЩС — щит слаботочный: ввод провайдера, роутер, коммутатор
- ПК — розетка компьютерная RJ45
- ТВ — розетка телевизионная
- ДФ — трубка или монитор домофона
- кабель от ЩС до точки, отдельным лучом
- мебель и сантехприборы подложка
- стояк: К1 — канализация, В1 — ХВС, Т3 — ГВС
- 1 — номер помещения, площадь м²

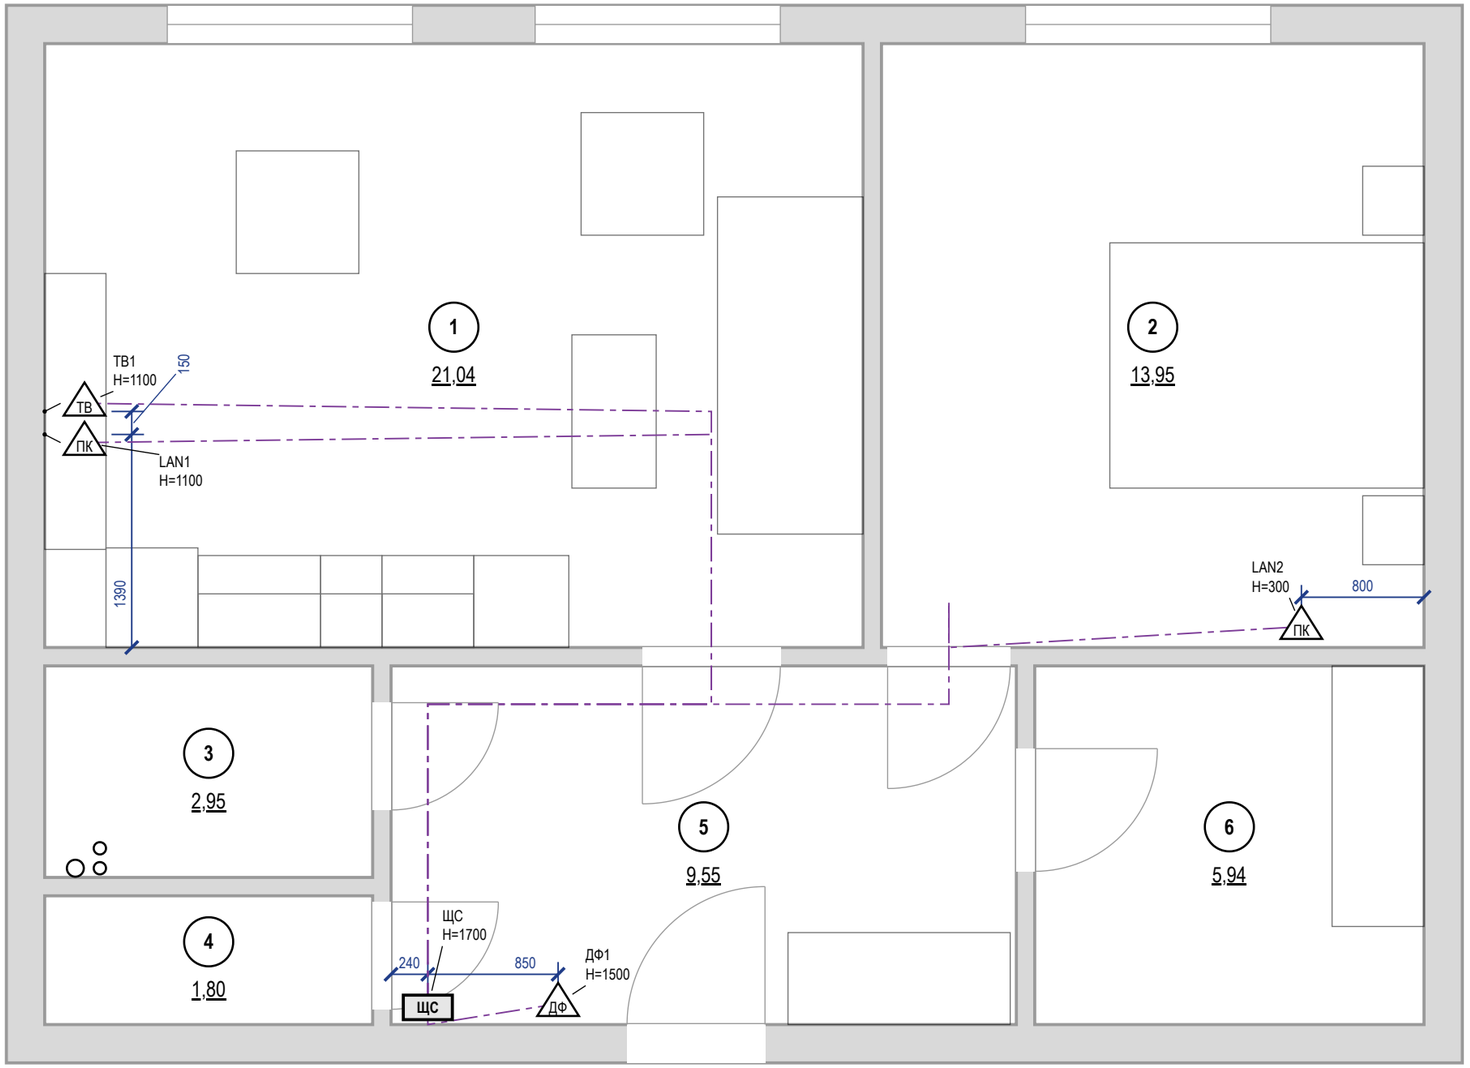

Примечания

1. За отметку 0,000 принят уровень чистого пола. Высоты H — от чистого пола до оси изделия; привязки — от чистовой грани стены до оси механизма (у рамки на несколько постов — до оси рамки).
2. Высота установки, не указанная на плане: розетки LAN и ТВ — 300 мм от чистого пола.
3. Слаботочные кабели — отдельно от силовых: в своей трубе или лотке, при параллельной прокладке не ближе 100 мм к силовым, пересечения под прямым углом; каждую точку — отдельным кабелем от ЩС без скруток.
4. Трассы на листе — принципиальные; фактические зафиксировать исполнительной схемой до закрытия отделкой. Силовые линии, УЗО 30 мА, ДСУП, кабель нг(А)-LS — по листам розеток и щита.
5. Проект силовой части и расчёт токов КЗ — по проекту ЭОМ; слаботочная часть согласуется с провайдером и управляющей компанией (домофон, коллективное ТВ).

	Лист	№ док.	Подпись	Дата
Дизайнер	Кырлан А.С.			04.11.26


Проект: Квартира 58 м² — **М 1:40**

План слаботочных сетей

Стадия	Лист	Листов
П	33	71

Условные обозначения

- светильник встраиваемый точечный
- линейный светильник настенный (подсветка столешницы), точка — вывод питания
- T° извещатель пожарный тепловой
- 1 номер помещения, площадь м²
- светильник потолочный накладной
- трековая система
- БП блок питания LED, с доступом (люк от 100×100 мм)
- светильник подвесной
- Св1·L1 марка светильника (как в ведомости и на развёртках) · группа включения L (лист 36)
- мебель и сантехприборы — подложка
- светильник настенный (бра), H — высота оси
- Д извещатель пожарный дымовой автономный
- стояк: К1 — канализация, В1 — ХВС, Т3 — ГВС

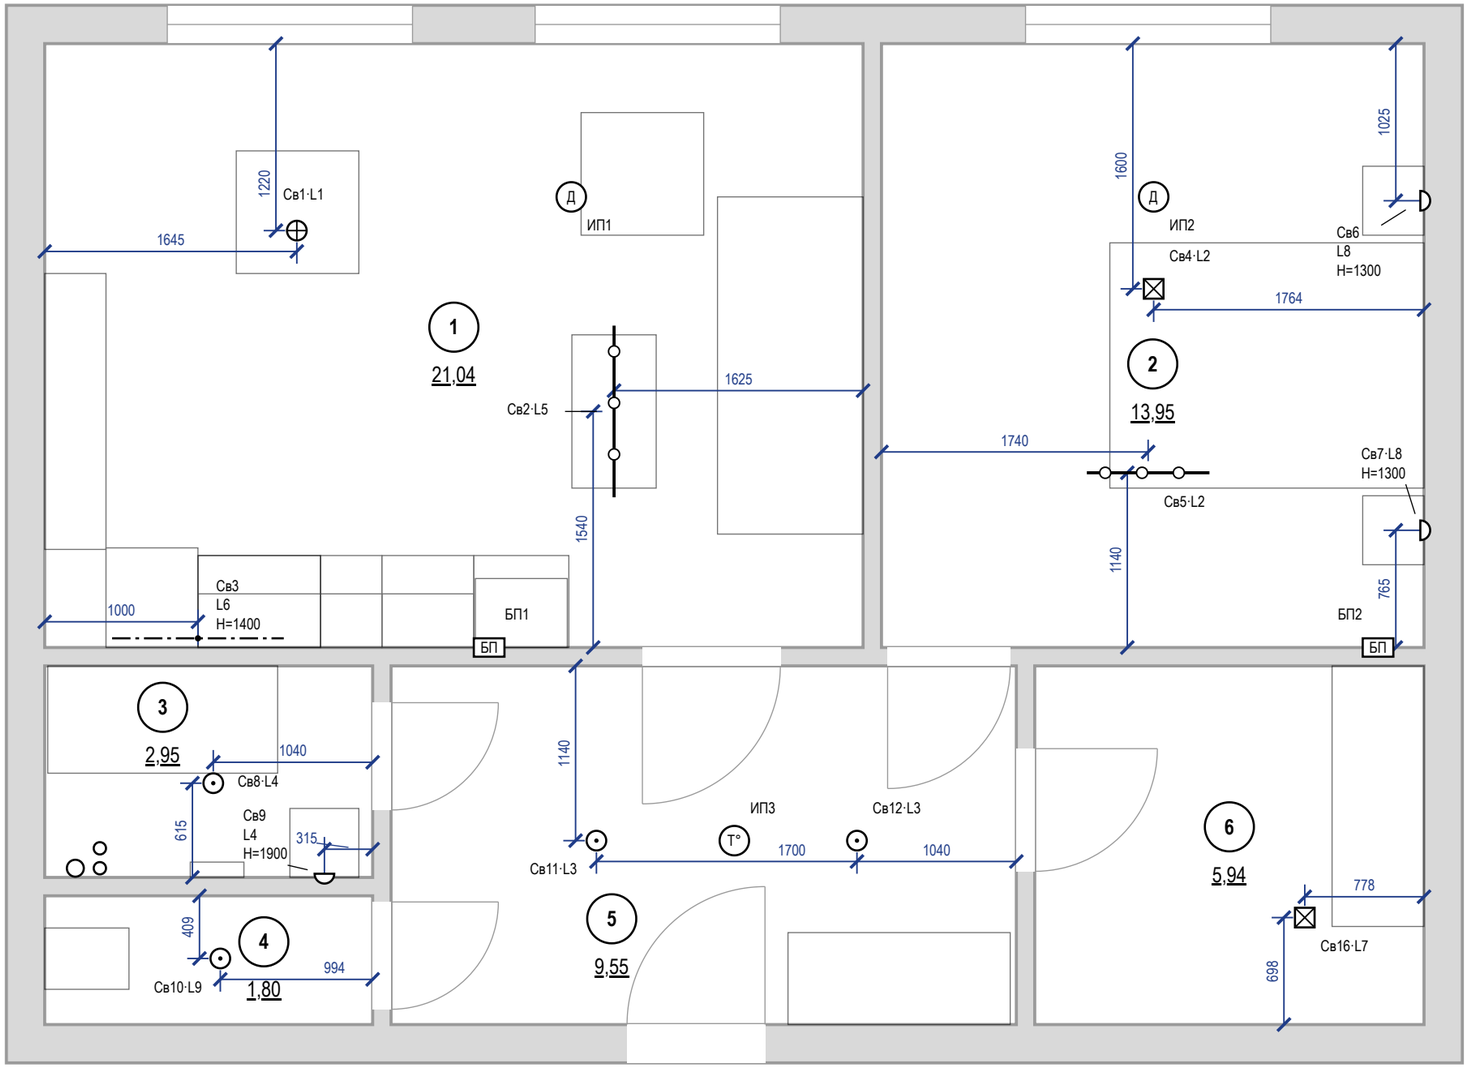

Примечания

1. За отметку 0,000 принят уровень чистого пола. Высоты H — от чистого пола до оси изделия; привязки — от чистовой грани стены до оси механизма (у рамки на несколько постов — до оси рамки).
2. Высота установки, не указанная на плане: светильники — на потолке; настенные — по отметке H у знака. Привязки — до оси светильника от чистовой грани стены, по рядам.
3. Во влажных помещениях — светильники не ниже IP44; в зонах 0–2 ванной — по ГОСТ Р 50571.7.701-2024 (зона 1 — IPX5).
4. Розеточные и мокрые линии — через УЗО или дифавтомат с током утечки не более 30 мА (ПУЭ 7.1.79); в санузле выполнить ДСУП (ПУЭ 7.1.87–7.1.88).
5. Кабель — медный, исполнение нг(A)-LS (ГОСТ 31565-2012); скрытая прокладка только горизонтально и вертикально, фактические трассы зафиксировать исполнительной схемой до закрытия отделкой.
6. Расчёт нагрузок, токов КЗ, селективности и сечений — по проекту ЭОМ организации с допуском СРО; лист задаёт состав, расположение и группы.
7. Ведомость светильников (тип, количество, мощность, поток, Tц, Ra) — лист 35.

					Проект: Квартира 58 м² — М 1:40
	Лист	№ док.	Подпись	Дата	План освещения
Дизайнер	Кырлан А.С.			04.11.26	Стадия: П · Лист: 34 · Листов: 71

Параметры светильников для подбора

Поз.	Марки	Наименование	Установка	Кол.	P, Вт	Σ P, Вт	Ф, лм	Тц, К	Ra	Угол, °	IP	Дим.	Слой	Группа	Пом.
1	Св1	Подвесной	подвес, низ H=1450	1	40	40	3600	3000	90	—	20	—	общий	L1	1
2	Св2	Трековая система	на потолке	4	12	48	950	3000	90	—	20	—	общий	L5	1
3	Св3	Линейный настенный	под верхними шкафами, H=1400	1	14	14	1080	3000	90	—	20	—	рабочий	L6	1
4	Св4	Потолочный накладной	на потолке	1	36	36	3200	2700	90	—	20	—	общий	L2	2
5	Св5	Трековая система	на потолке	2	12	24	900	2700	90	—	20	—	общий	L2	2
6	Св6, Св7	Настенный (бра)	на стене, H=1300	2	4	8	250	2700	90	—	20	—	рабочий	L8	2
7	Св8	Встраиваемый точечный	в ГКЛ, корпус ≤ 70 мм	1	9	9	700	3000	90	—	44	—	общий	L4	3
8	Св9	Настенный (бра)	над зеркалом, H=1900	1	6	6	400	3000	90	—	44	—	рабочий	L4	3
9	Св10	Встраиваемый точечный	в ГКЛ, корпус ≤ 70 мм	1	6	6	500	3000	90	—	44	—	общий	L9	4
10	Св11, Св12	Встраиваемый точечный	в ГКЛ, корпус ≤ 70 мм	2	9	18	800	3000	90	—	20	—	общий	L3	5
11	Св16	Потолочный накладной	на потолке, засветка стены	1	10	10	900	3000	90	—	20	—	общий	L7	6
		Итого		**17 шт**		**219**									

LED-ленты, линейные светильники и блоки питания

Марка	Пом.	L, м	U, В	Вт/м	Σ P, Вт	БП	P БП, Вт	Загр., %	Питание	Доступ к БП
Св2	1	1,2	24	—	48	БП1	100	62	встроенный ввод	H=2300
—	1	1,8	24	—	14	БП1	100	62	встроенный ввод	H=2300
Св5	2	0,8	24	—	24	БП2	60	40	встроенный ввод	H=2300

Примечания


1. Позиции и марки Св — те же, что на плане освещения (лист 34); группы L — по плану выключателей (лист 36).
2. Модели светильников не выбраны: лист — техническое задание на подбор. Модель по строке таблицы: поток, Тц, Ra, угол, IP и регулировка яркости не хуже указанных, мощность не больше; встраиваемые — под глубину короба (графа «Установка»). IP 20 — сухие помещения. После выбора моделей (артикул, производитель) лист выпускается как «Спецификация светильников».
3. Мощность и поток в таблице — требования к подбору (поток не меньше, мощность не больше указанных); после выбора модели — по её паспорту, Σ P — установленная мощность освещения. Оценка освещённости — на плане освещения; это не светотехнический расчёт.

					Проект: Квартира 58 м²
	Лист	№ док.	Подпись	Дата	
Дизайнер	Кырлан А.С.			04.11.26	Техническое задание на подбор светильников

Стадия	Лист	Листов
П	35	71

Условные обозначения

- выключатель одноклавишный
- выключатель с проходной или перекрёстной клавишей (обратный флажок); тип клавиши — в подписи
- S1 → марка → группы по клавишам (через «;»): прох. — проходной, перекр. перекрёстный, дим. — светорегулятор; H — высота
- связь: выключатель → ближайший светильник группы в том же помещении (не трасса кабеля); полный состав группы — по номеру L
- светильник встраиваемый точечный
- светильник потолочный накладной
- светильник подвесной

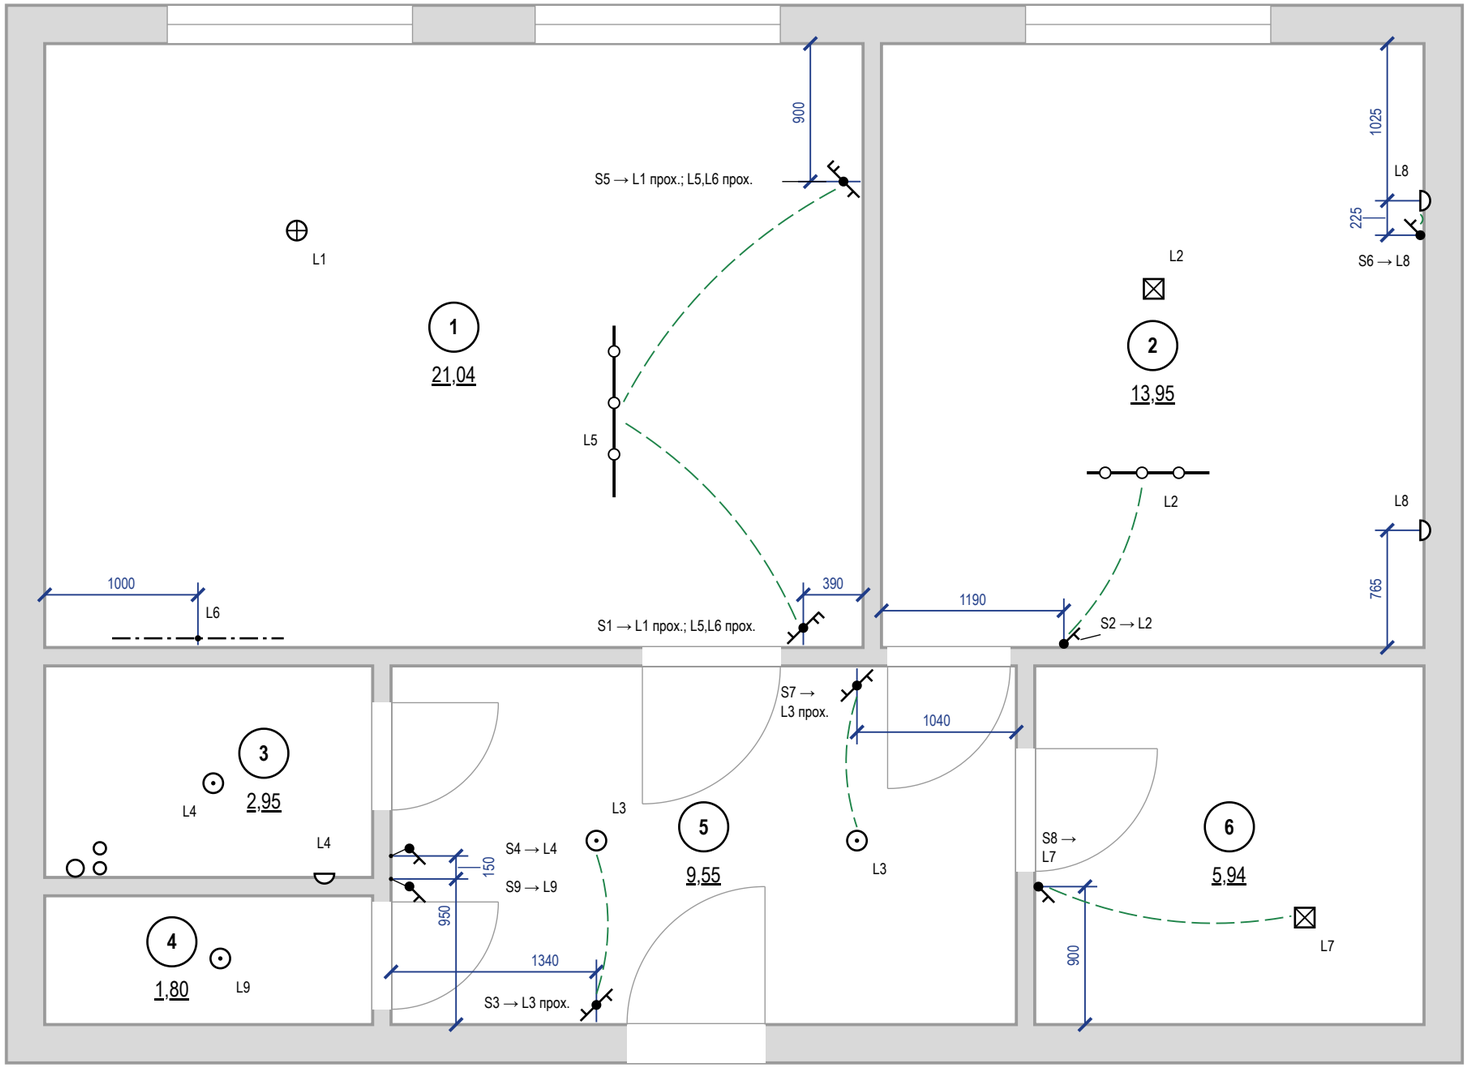


Примечания

1. За отметку 0,000 принят уровень чистого пола. Высоты H — от чистого пола до оси изделия; привязки — от чистовой грани стены до оси механизма (у рамки на несколько постов — до оси рамки).
2. Высота установки, не указанная на плане: выключатели — 900 мм от чистого пола (у кровати и другие — H у марки), со стороны дверной ручки (ПУЭ 7.1.51).
3. Какой выключатель какие светильники включает — по номеру группы L: у выключателя (S1 → L1; L2 — клавиши по порядку) и у каждого светильника. Пунктир подсказка к ближайшему светильнику группы в том же помещении (не дальше 3 м), это не трасса кабеля; выключатель за стеной (у двери санузла) и далёкая группа — только номер группы.
4. Группы из нескольких мест (L1 — S1, S5; L5 — S1, S5; L6 — S1, S5; L3 — S3, S7): на крайних местах — проходные клавиши, на промежуточных — перекрёстные; механизмы — в ведомости изделий.
5. Вентиляторы санузлов (выводы ЭВ на плане розеток) включаются вместе с основным светом помещения, отключаются с задержкой — таймер выбега в вентиляторе.
6. Розеточные и мокрые линии — через УЗО или дифавтомат с током утечки не более 30 мА (ПУЭ 7.1.79); в санузле выполнить ДСУП (ПУЭ 7.1.87–7.1.88).
7. Кабель — медный, исполнение нг(A)-LS (ГОСТ 31565-2012); скрытая прокладка только горизонтально и вертикально, фактические трассы зафиксировать исполнительной схемой до закрытия отделкой.
8. Расчёт нагрузок, токов КЗ, селективности и сечений — по проекту ЭОМ организации с допуском СРО; лист задаёт состав, расположение и группы.

Условные обозначения (окончание)

- светильник настенный (бра), H — высота оси
- линейный светильник настенный (подсветка столешницы), точка — вывод питания
- трековая система
- L1 — группа включения у светильника
- стояк: К1 — канализация, В1 — ХВС, Т3 — ГВС
- 1 — номер помещения, площадь м²

					Проект: Квартира 58 м²	М 1:40
	Лист	№ док.	Подпись	Дата	Управление светильниками	Стадия / Лист / Листов
Дизайнер	Кырлан А.С.			04.11.26		П / 36 / 71

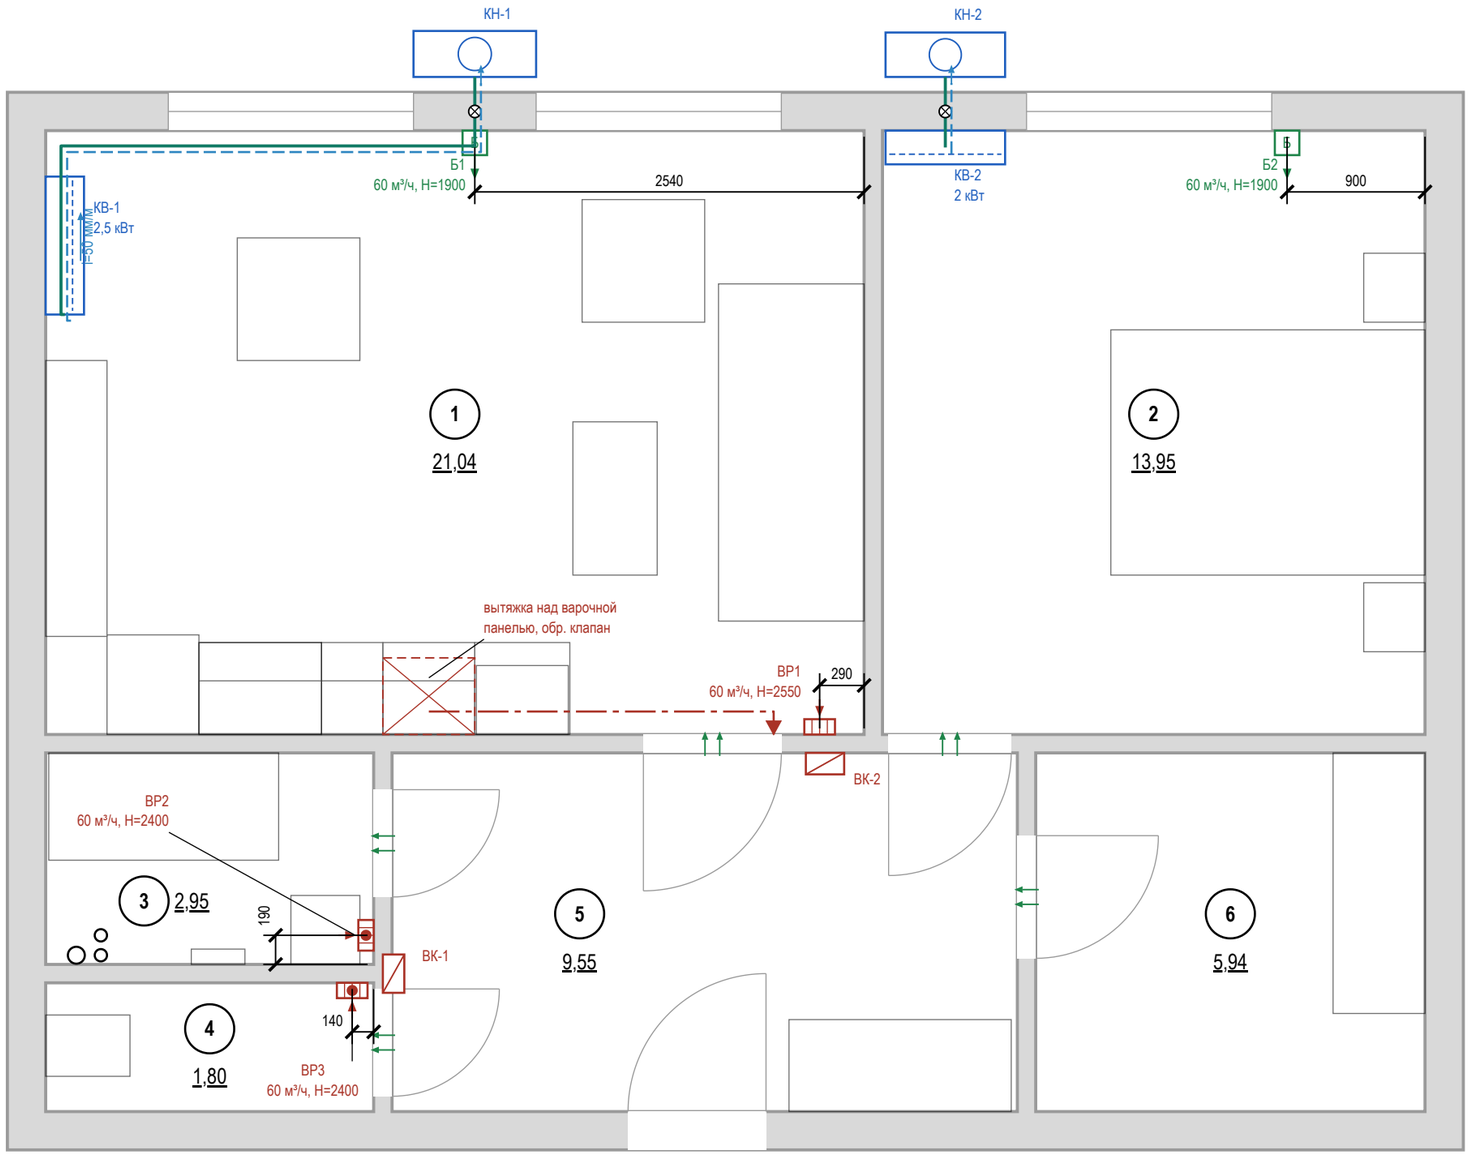

Условные обозначения

- стояк: К1 — канализация, В1 — ХВС, Т3 — ГВС
- номер помещения, площадь м²
- вытяжная решётка в вентканал: марка, расход м³/ч, Н центра от чистого пола
- вытяжная решётка с бытовым вентилятором и обратным клапаном: марка, расход, Н
- бризер (приток с фильтром и подогревом)
- переток: зазор под полотном или переточная решётка
- кухонная вытяжка над варочной панелью
- Вентканал ВК-N.
- воздуховод кухонной вытяжки в коробе под потолком
- отдельный вход воздуховода в вентканал, обратный клапан
- внутренний блок кондиционера (КВ-N)
- наружный блок (КН-N) на фасаде / в корзине
- трасса фреонопровода и межблочного кабеля
- дренаж конденсата (уклон стрелкой)
- отверстие в наружной стене под трассу

Воздухообмен, м³/ч

№	Помещение	Выт. норма	Выт. проект	Прит. норма	Прит. проект	Устрой-ства
1	Кухня-гостиная	60	60	60	60	ВР1, Б1
2	Спальня			60	60	Б2
3	Ванная	50	60			ВР2
4	Санузел	25	60			ВР3
6	Гардеробная	3				переток
	Итого	**138**	**180**	**120**	**120**	
	Норма по жильцам: 30×2			60		

Воздухообмен квартиры — по большей из сумм притока и вытяжки: норма 138 м³/ч, проект 180 м³/ч.
Вытяжка не меньше притока — баланс сведён.

Кондиционеры

Марка	Помещение	Нар. блок	Трасса, м	Дренаж
КВ-1	1. Кухня-гостиная	КН-1	3,0	наружу, i=50 мм/м
КВ-2	2. Спальня	КН-2	3,0 п	наружу, i=50 мм/м

Привязки — до обмера
Вентканалы ВК-N приняты проектировщиком, решётки и воздуховоды — от них. До черновых работ — обмер каналов и тяги, лист перевыпустить по факту.

Примечания


1. Расчёт систем ОВ и подбор оборудования — проектная организация с допуском СРО; лист даёт места, трассы и привязки.
2. Нормы вытяжки — СП 54.13330.2022 (Изм. 1, 2), табл. 7.1: кухня с электроплитой 60 м³/ч, с газовой 100; ванная и совмещённый санузел 50; уборная 25; гардеробная 0,2 ч⁻¹. Приток в жилые — 3 м³/ч на 1 м² (менее 20 м² общей площади на человека), иначе 30 м³/ч на человека.
3. Вентканалы и шахты не сужать, не переносить и не закрывать; вентилятор и кухонная вытяжка — через обратный клапан, без перекрытия естественной тяги.
4. Кухонная вытяжка в воздухообмен не включена: воздуховод не менее Ø125 в коробе, вход в канал отдельный.
5. Переток — зазор под полотнами межкомнатных дверей или переточная решётка.
6. Дренаж кондиционера — непрерывный уклон 40–60 мм/м без контруклонов (СТО НОСТРОЙ 2.23.1-2011, п. 5.8.4); врезка в К1 — через сифон (п. 5.8.9); длина трассы и перепад высот — по паспорту блока; внутренний блок — не ближе 150 мм к потолку, не над кроватью и рабочим местом.
7. Наружный блок на фасаде многоквартирного дома — с согласия собственников (общее имущество); при наличии корзин — только в них.
8. «п» в графе «Трасса» — трасса фреона по плану короче минимума, разница выбрана компенсационной петлёй (бухтой): КВ-2 — по плану 0,8 м, с петлёй 3,0 м. Длина петли принята по минимуму трассы (3,0 м) и зависит от паспорта модели кондиционера, которая ещё не выбрана: минимум и максимум трассы — типовые, по паспорту модели, до заказа сверить и при необходимости изменить петлю или место наружного блока. Бухту уложить в коробе или за внутренним блоком, не в штробе.
9. Привязки оборудования — по паспортам приобретённых моделей, до черновых работ.

	Лист	№ док.	Подпись	Дата
Дизайнер	Кырлан А.С.			04.11.26

Проект: Квартира 58 м² — **М 1:40**

План вентиляции

Стадия	Лист	Листов
П	37	71

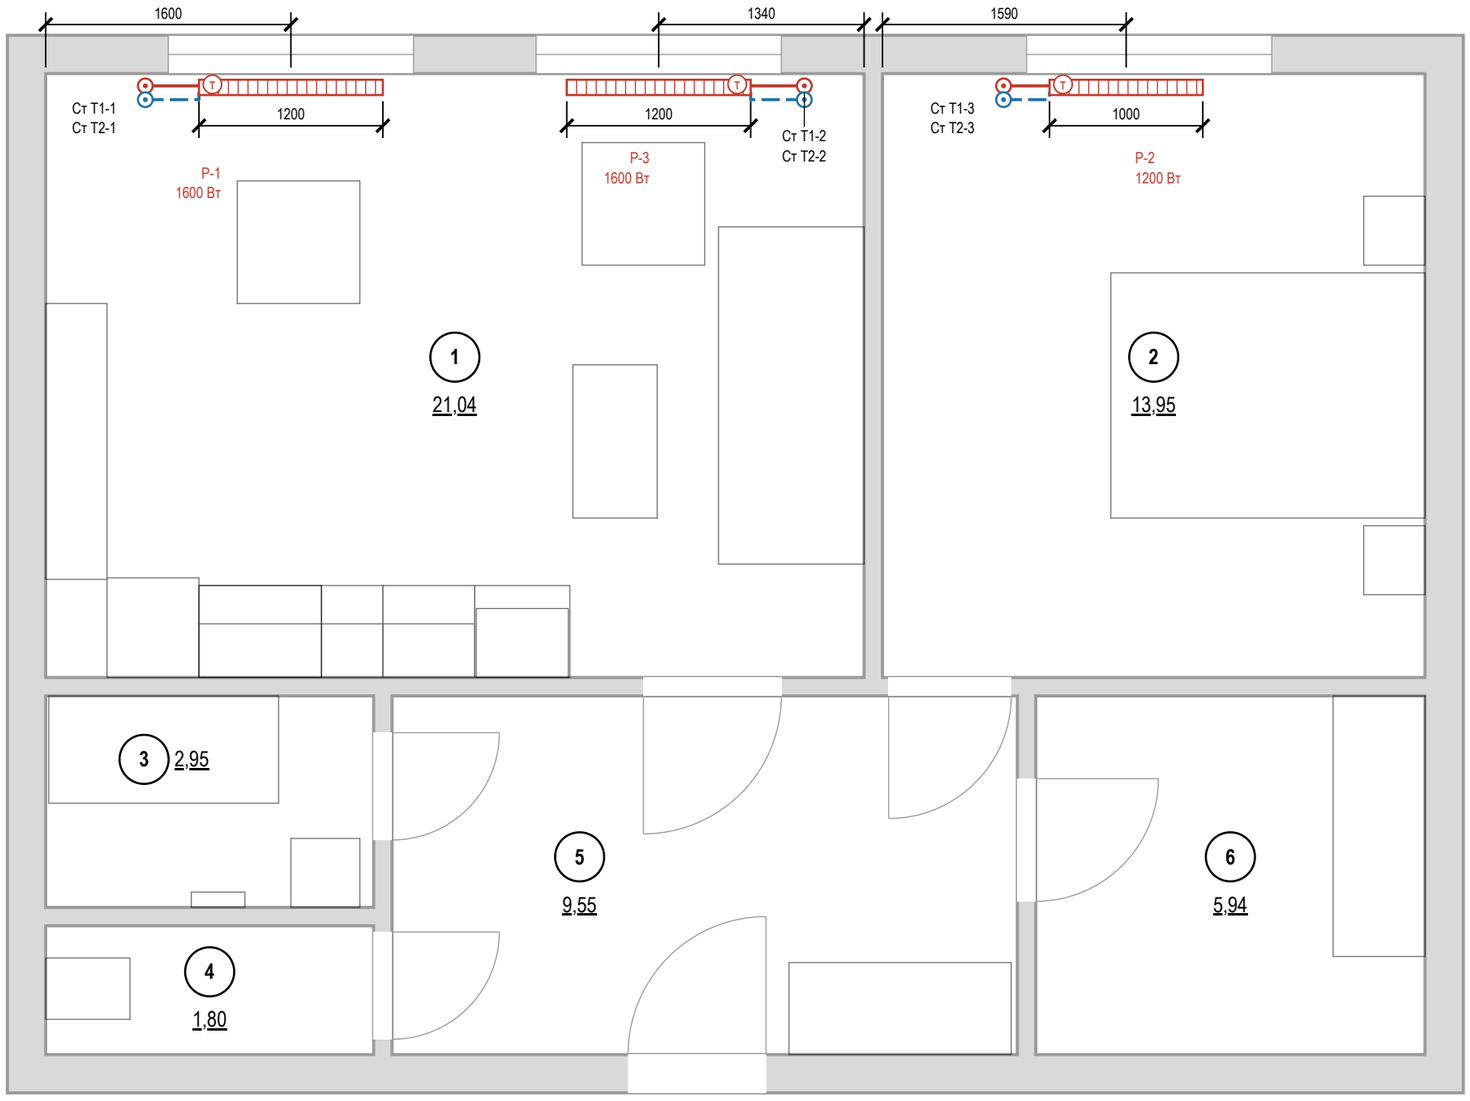

Условные обозначения

- 1 — номер помещения, площадь м²
- радиатор отопления (марка РО-N, длина по плану)
- Т — клапан с термоголовкой на подаче
- стояк отопления, подающий (Ст Т1-N)
- стояк отопления, обратный (Ст Т2-N)
- Т1 — отопление, подающий трубопровод
- Т2 — отопление, обратный трубопровод

Ведомость радиаторов

Марка	Помещение	Тип	Д×В×Г, мм	Низ / стена	Q, Вт
Р-1	1. Кухня-гостиная	панельный 22	1200×500×100	120 / 40	1600
Р-3	1. Кухня-гостиная	панельный 22	1200×500×100	120 / 40	1600
Р-2	2. Спальня	панельный 22	1000×500×100	120 / 40	1200

Низ — от чистого пола, стена — зазор до задней панели, мм.

Привязки — до обмера


Стояки отопления в исходных данных не заданы: показаны у откосов окон, подводки — принципиально. До черновых работ — обмер стояков и паспорта приборов; лист перевыпустить по факту.

Примечания




1. Расчёт системы отопления, теплопотерь и подбор приборов — проектная организация с допуском СРО; лист даёт места и привязки.
2. Тип, длина и мощность радиаторов — по теплотехническому расчёту; лист задаёт места, зазоры и подключение.
3. Зазоры радиатора: низ не менее 100 мм от чистого пола, верх не менее 100 мм до подоконника, 30–50 мм от стены до задней панели; центр по оси окна с допуском ±20 мм. Верх до подоконника — 180 мм.
4. Радиаторы не закрывать глухими коробами и мебелью; перенос и замена приборов в многоквартирном доме — переустройство, согласование с управляющей организацией (ЖК РФ ст. 25–26); вынос на лоджию запрещён.
5. Трубы отопления через межквартирные стены не прокладывать (СП 51.13330.2011, п. 9.19); через перекрытия и перегородки — в гильзах.
6. Привязки приборов и подводок — по паспортам приобретённых радиаторов и клапанов, до черновых работ.
7. До закрытия отделкой трубопроводы отопления испытать гидростатическим давлением с оформлением акта (СП 73.13330.2016, 7.2–7.3).

					Проект: Квартира 58 м² — **М 1:40**
	Лист	№ док.	Подпись	Дата	
Дизайнер	Кырлан А.С.			04.11.26	План отопления — Стадия: П; Лист: 38; Листов: 71

выпуск 04.11.2026 № e0dc2f2b59 · стр. 38 из 71

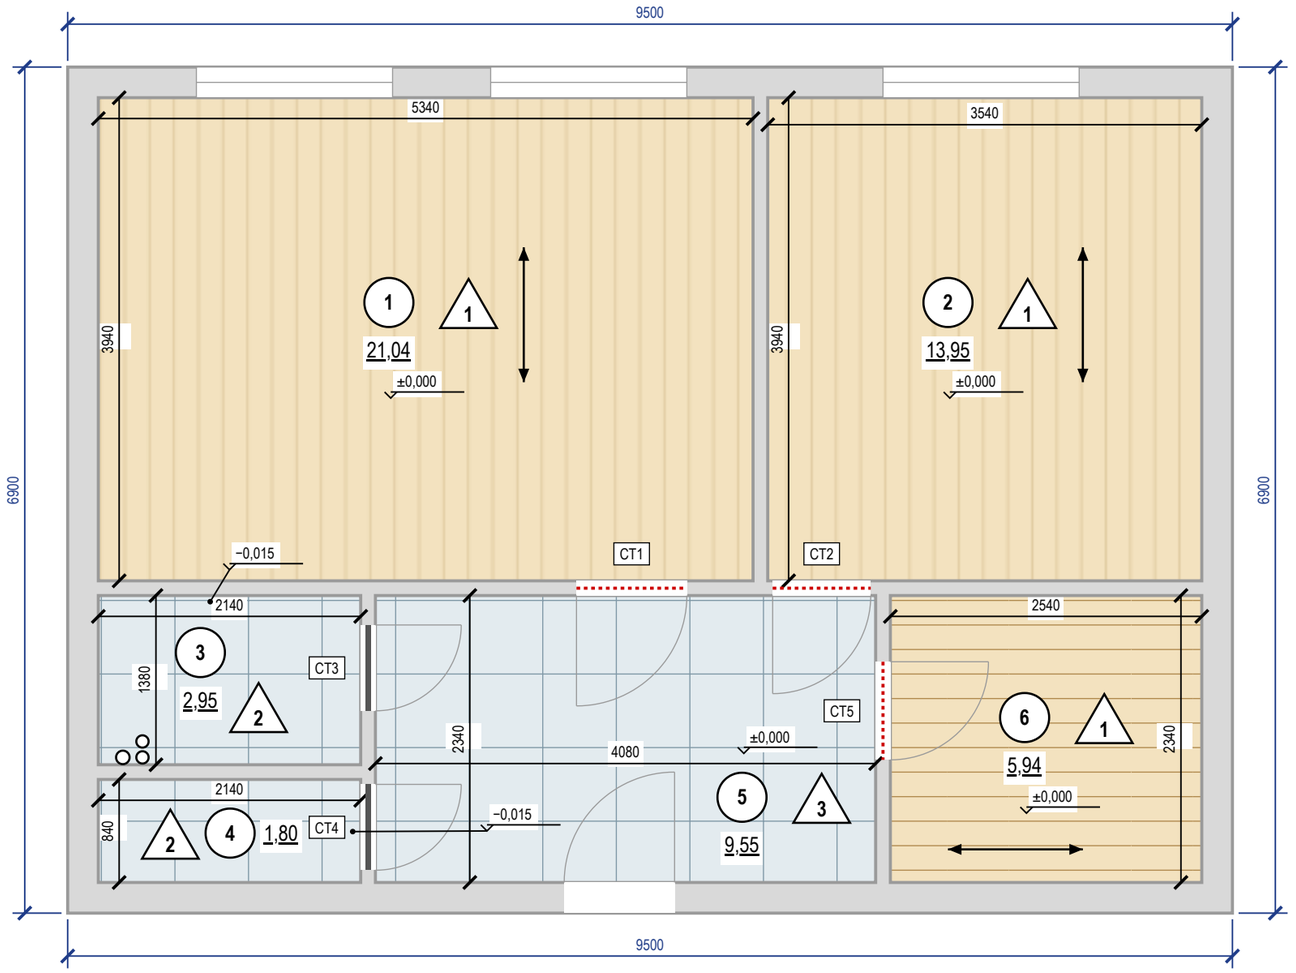

Экспликация полов

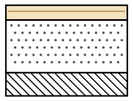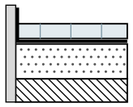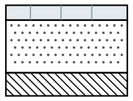Номер помещения	Тип пола	Схема пола	Данные элементов пола (наименование, толщина, основание), мм	Площадь, м²
1, 2, 6	1		Инженерная доска на клею — 14 Стяжка ЦПС М200 — 50 Плита перекрытия Всего 64 мм; ЧП ±0,000, верх плиты −0,064	40,93
3, 4	2		Керамогранит на клею С2 TE S1 — 14 Гидроизоляция обмазочная, 2 слоя, с заведением на стены 200 мм — 2 Стяжка ЦПС М200 — 33 Плита перекрытия Всего 49 мм; ЧП −0,015, верх плиты −0,064	4,75
5	3		Керамогранит на клею С2 TE S1 — 14 Стяжка ЦПС М200 — 50 Плита перекрытия Всего 64 мм; ЧП ±0,000, верх плиты −0,064	9,55
			Итого	**55,23**

Раскладка покрытий

Пом.	Укладка	Старт (оси от чистовых стен), мм	Отступ 1-го ряда / крайние плитки, мм
1	вдоль стен Б/Г, прямая	от стены Г, 1-й ряд вдоль неё	зазор от стены не задан
2	вдоль стен Б/Г, прямая	от стены Г, 1-й ряд вдоль неё	зазор от стены не задан
3	плитка	раскладка плиточника не задана	
4	плитка	раскладка плиточника не задана	
5	плитка	раскладка плиточника не задана	
6	вдоль стен А/В, прямая	от стены А, 1-й ряд вдоль неё	зазор от стены не задан

Спецификация плинтусов

Наименование	Помещения	Длина, м (с запасом)
SX184, h = 110 мм, крепление к стене, окраска в цвет NCS S 0300-N	1, 2, 5	44
SX184, h = 110 мм, крепление к стене, окраска в цвет Tikkurila V503	6	10

Примечания

1. За отметку ±0,000 принят чистый пол, не существующий (блок отметок). Площади — по чистым размерам помещений, м²; размеры — в мм.
2. Стык разнотипных покрытий — по оси дверного полотна (под полотном в закрытом положении); решение стыка — по ведомости стыков.
3. Пол санузлов ниже смежных помещений на 15 мм за счёт меньшей толщины стяжки (верх плиты общий — по экспликации полов); гидроизоляция по стяжке с заведением на стены не менее 200 мм (СП 29.13330.2011, п. 7.2), до облицовки — тест проливом и акт скрытых работ.
4. Трубопроводы в конструкции пола не прокладываются: пирог пола 49–64 мм не вмещает выпуски канализации с уклоном — выпуски К1 ведутся по стенам над чистым полом в коробах (лист 15).
5. Звукоизоляционный слой под стяжкой проектом не предусмотрен (стяжка по плите): приведённый уровень ударного шума перекрытия с полом Lnw не более 60 дБ (СП 51.13330.2011, табл. 2) подтвердить по данным дома; при превышении — плавающая стяжка по звукоизоляции с демпферной лентой по контуру и у стояков, пирог пересчитать.
6. Штучные покрытия (инженерная доска): направление — по стрелке; влажность основания по СМ не более 2,0 % (по ТУ изготовителя).
7. Ровность основания — просвет под 2-метровой рейкой не более 2 мм: пом. 1, 2, 6 (инженерная доска), пом. 3, 4, 5 (керамогранит); проверить до укладки покрытия (СП 71.13330.2017, табл. 8.5).
8. Сетка на плитке — условная, в размер формата; точка старта и раскладка — по листу раскладки плитки.
9. Узор покрытия (заливка-код типа пола) прерывается под надписями — площадями помещений и отметками чистого пола.
10. Пироги полов — по экспликации полов: слои сверху вниз, толщины в мм; гидроизоляция мокрых зон — в пироге и в ведомости отделки; схема пола — без масштаба.

Отметки по высоте

±0,000 чистый пол пом. 1, 2, 5, 6; отсчёт высот
−0,015 чистый пол пом. 3, 4, ниже на 15 мм
−0,064 верх плиты — расчёт, не замер (задание на обмер)
сущ. пол снимается до плиты; не замерен (задание на обмер)


	Лист	№ док.	Подпись	Дата
Дизайнер	Кырлан А.С.			04.11.26

Проект: Квартира 58 м² — **М 1:50**


План покрытий пола

Стадия	Лист	Листов
П	39	71

Фрагмент 1. Ванная (пом. 3). Пол 600×600, шов 2 мм, М 1:20

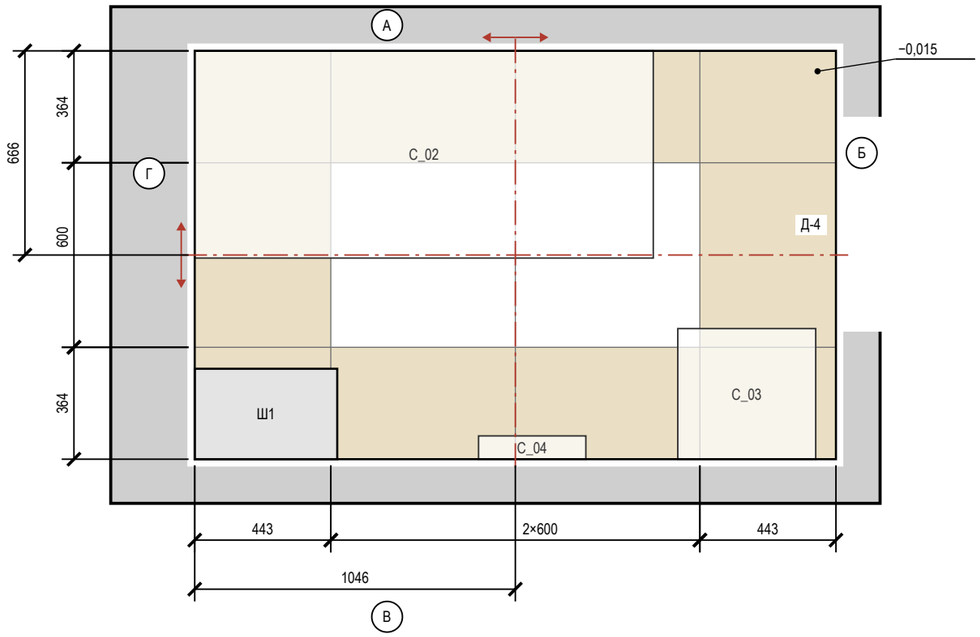

Фрагмент 2. Санузел (пом. 4). Пол 600×600, шов 2 мм, М 1:20

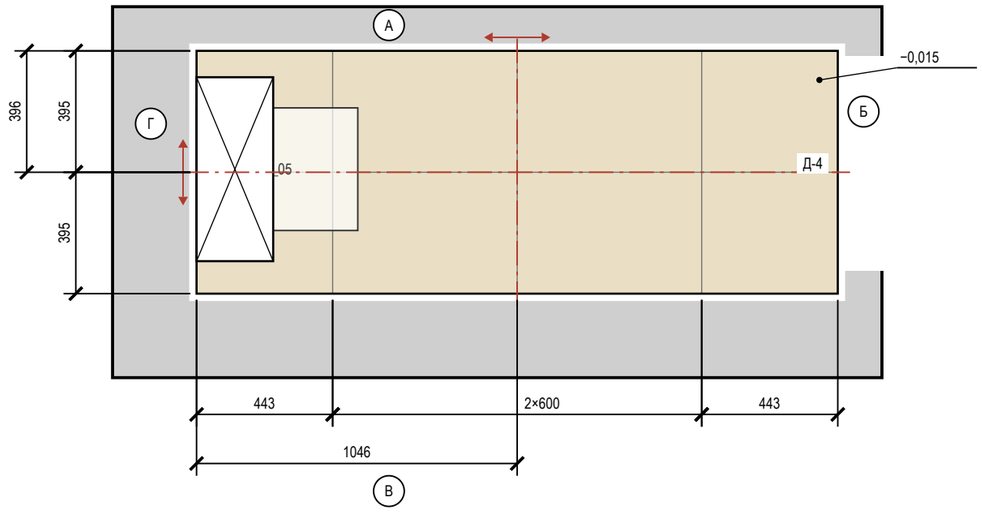

Ведомость материалов

Материал	Класс, код	Норма расхода	Кол-во
Затирка	класс не задан	(a+b)/ab·шов·t·1,6	3,9 кг
Клей	С2 S1	1,5 кг/м²·мм, слой 5	35 кг (2 меш.)
Клей	С2	1,5 кг/м²·мм, слой 5	332 кг (14 меш.)
Гидроизоляция	обмазочная, 2 слоя: пол, стены по периметру и зоны замачивания	по ТУ	13,4 м²
Демпф. лента	по периметру пола из плитки		21,0 м

Ведомость плитки

Помещение, поверхность	Плитка, код	Формат	Шов	S, м²	Целых	Подр.	С запасом
Ванная, пол	SG651622R	600×600	2	2,95	2	10	14
Ванная, стены А–Г	610015000370	1200×600	2	14,95	0	40	44
Ванная, короб стояков Ш1 489×319	610015000370	1200×600	2	1,99	0	10	12
Санузел, пол	SG651622R	600×600	2	1,80	0	8	9
Санузел, стены А–Г	610015000370	1200×600	2	13,40	0	30	34
Санузел, короб инсталляции	610015000370	1200×600	2	1,47	0	7	8
Прихожая, пол	SG651622R	600×600	2	9,55	10	18	31
Итого 600×600				14,30	12	36	54
Итого 600×1200				**31,80**	**0**	**87**	**98**

Условные обозначения


- плитка целая; тонкая линия — шов
- плитка с подрезкой (размер — на цепочке)
- ось старта; стрелки — направление укладки
- сантехприбор: габарит, высота по практике
- короб инсталляции: плитка пола — до короба
- короб стояков (Ш…): плитка пола — до короба
- отметка чистого пола на полке выноски, м
- (А) обозначение стены А–Г (как на развёртках)

Примечания

1. Раскладка от чистовых размеров: стены санузлов теряют 10 + 5 + 9 = 24 мм на сторону (штукатурка, клей, плитка); подрезки — чистые, без шва.
2. Старт — от центра помещения (штрихпунктир, стрелки — направление укладки); размер старта — от чистовых стен Г и А.
3. Раскладка пола «Прихожая» — на листе «Раскладка плитки. Прихожая».
4. Калибр партии не задан — до укладки замерить (рабочий размер W, ГОСТ 13996-2019) и пересчитать подрезки.
5. Количество: целые по раскладке + по одной на подрезку, запас 10 %; один артикул — одна партия и тон. Исключены поддон, короб, проёмы и места за коробом; S — по чистым граням: стены нетто = зона облицовки по ведомости отделки − место за коробом инсталляции 2,71 м² (плитку за коробом не кладут), короб — отдельной строкой.
6. Клей С2 S1; С2 (ГОСТ Р 56387-2018), затирка класс не задан; расход — по ТУ выбранной марки.
7. Гидроизоляция: пол и стены 200 мм от ЧП; над ванной — до 2000 и 300 мм за борт (пом. 3) (см. развёртки); акт скрытых работ, пролив 24 ч.
8. Отметка чистого пола −0,015, порог 15 мм; стык с соседним покрытием — по оси полотна двери.

					Проект: Квартира 58 м²		**М 1:20**
	Лист	№ док.	Подпись	Дата	Раскладка плитки. Планы полов	Стадия	Лист	Листов
Дизайнер	Кырлан А.С.			04.11.26		П	40	71

Фрагмент 1. Прихожая (пом. 5). Пол 600×600, шов 2 мм, М 1:20

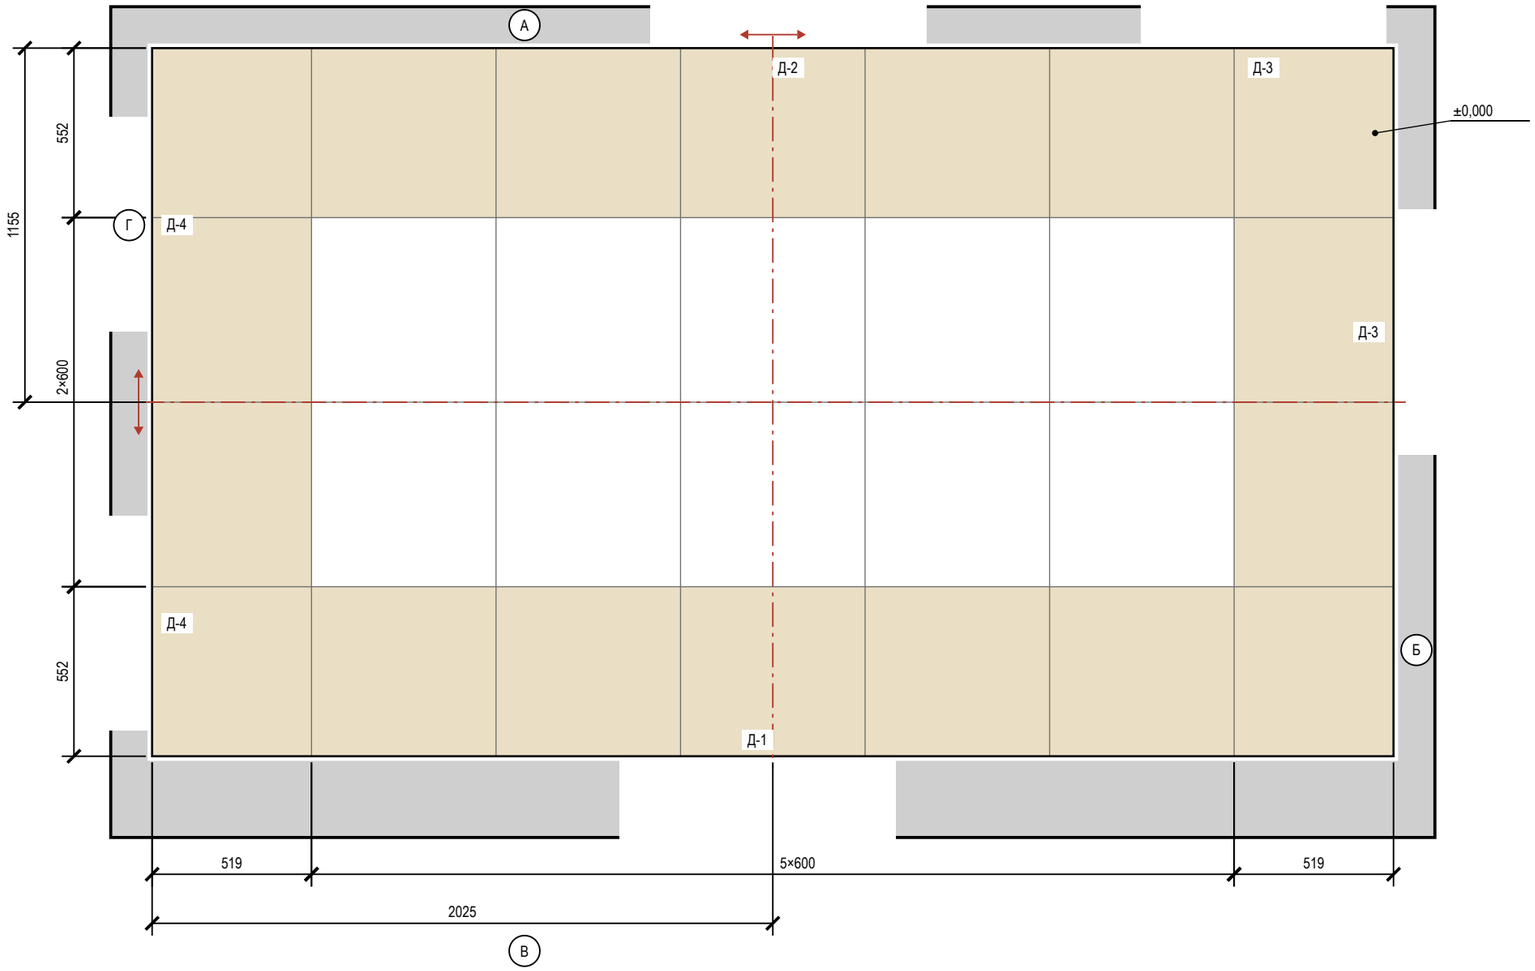

Условные обозначения

- плитка целая; тонкая линия — шов
- плитка с подрезкой (размер — на цепочке)
- ось старта; стрелки — направление укладки
- отметка чистого пола на полке выноски, м
- (А) обозначение стены А–Г (как на развёртках)

Подсчёт плитки


Поверхность	Формат	S, м²	Целых	Подр.	С запасом
Прихожая, пол	600×600	9,55	10	18	31

Примечания

1. Прихожая: керамогранит 600×600, длинная сторона — вдоль стен Б и Г, шов 2 мм, прямая раскладка от центра. Стены окрашены: раскладка от чистового контура минус штукатурка и шпаклёвка 15 мм на сторону (принято); подрезки 519 / 552 мм, срез — под плинтус.
2. Прихожая: деформационный зазор по периметру 8–10 мм под плинтусом; в проёмах — стык с соседним покрытием по оси полотна двери. Клей С2, затирка класс не задан.
3. Клей, затирка и итог по форматам — в ведомостях листа «Раскладка плитки. Планы полов».


					Проект: Квартира 58 м² — М 1:20
	Лист	№ док.	Подпись	Дата	
Дизайнер	Кырлан А.С.			04.11.26	Раскладка плитки. Прихожая
					Стадия: П; Лист: 41; Листов: 71

Развёртка стены В

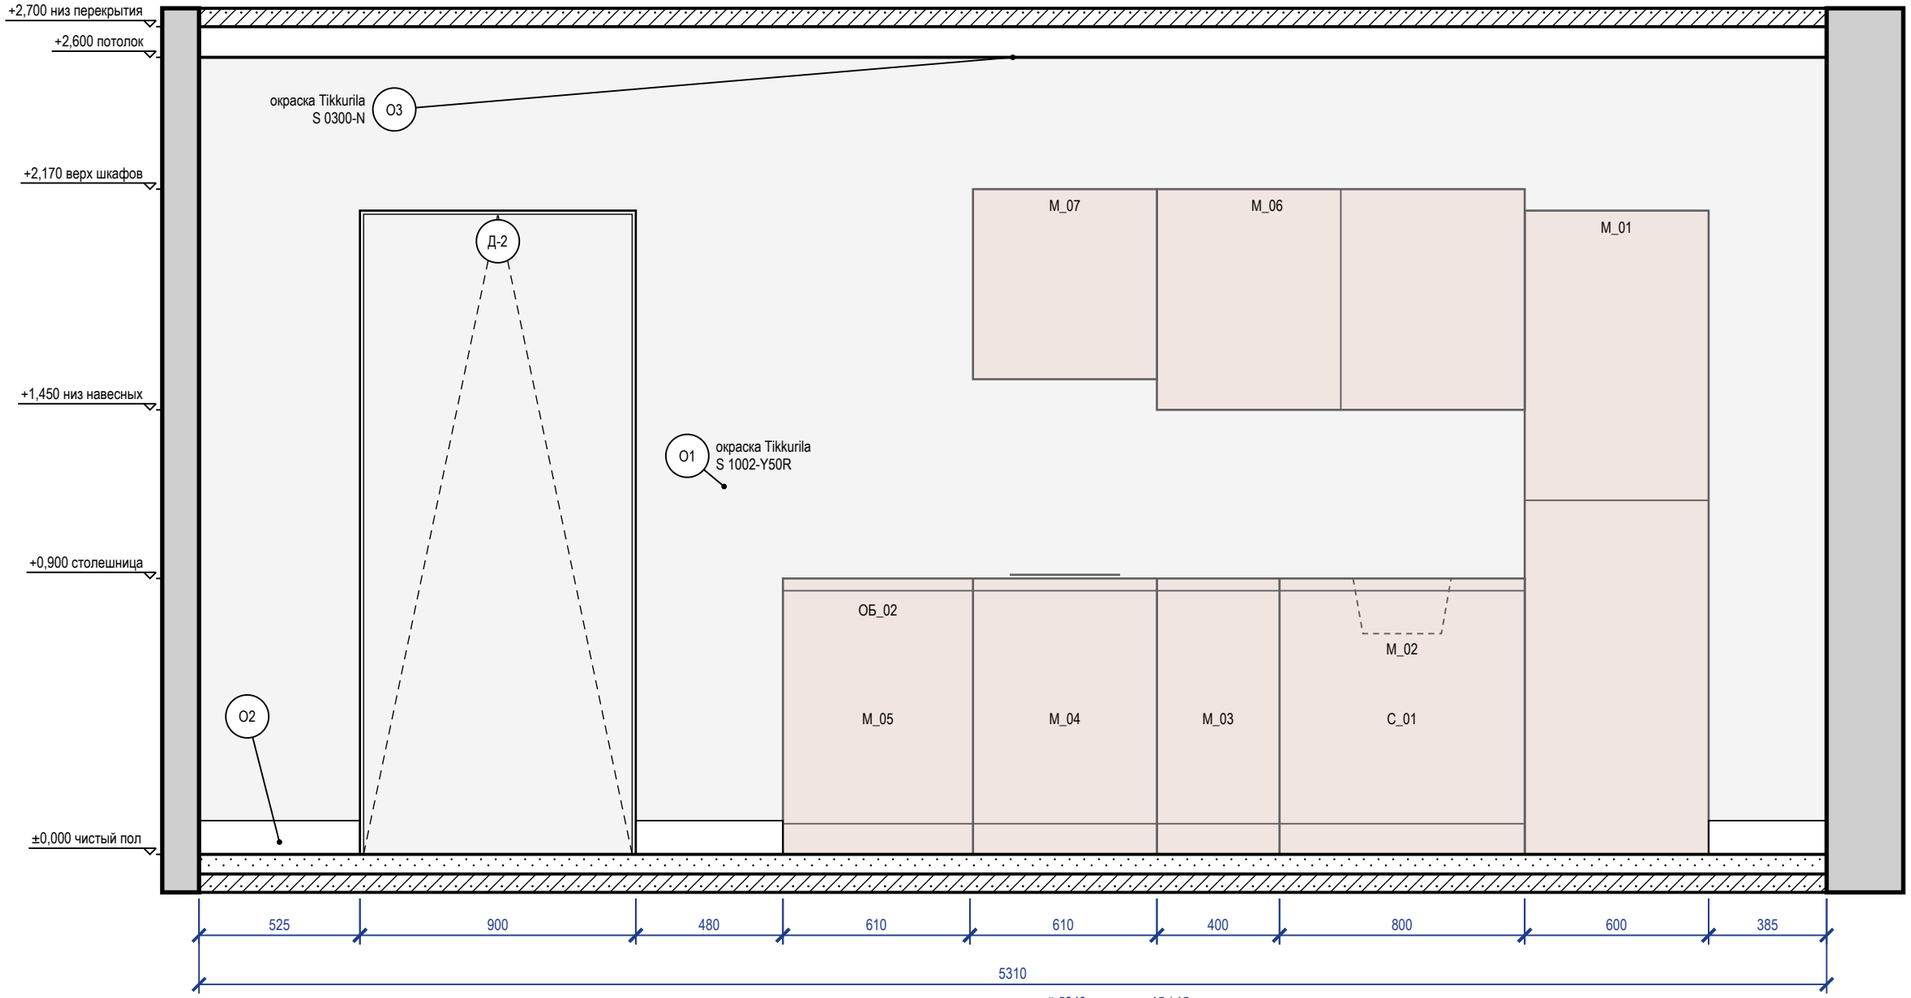

между чистовыми гранями: черновой 5340 − отделка 15 / 15

Схема развёрток (М 1:100)

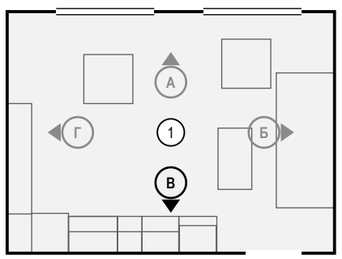

Ведомость отделки (на листе)

Марка	Поверхность	Материал, изделие	Цвет, код	Кол.
О1	стены	окраска, Tikkurila, шелковисто-матовая, подготовка Q3	NCS S 1002-Y50R	11,9 м²
О2	плинтус	плинтус МДФ, Orac Decor Luxxus, h 110 мм, SX184, шелковисто-матовая	NCS S 0300-N	1,4 м
О3	потолок	окраска, Tikkurila, глубокоматовая	NCS S 0300-N	21 м²

Примечания

1. Размеры — в мм от чистовых поверхностей стен; условные обозначения и общие указания — лист 3.
2. Стена В показана двумя видами: здесь — архитектурная развёртка (мебель, отделка, проёмы, высоты), электроточки и выводы ВК с привязками и таблицей — на листе 43 («Привязки»).
3. Двери скрытого монтажа — полотно в плоскости стены, отделка стены по полотну, плинтус прерывается у короба (узел — на листе узлов).
4. Потолок — у каждой стены свой, по плану потолков (ПТ2); ступени — зоной, кромка короба перед нишей — тонкой линией; в поле потолка: ПТ1 +2,550.

					Проект: Квартира 58 м²	М 1:20
	Лист	№ док.	Подпись	Дата	Развёртка стены В. Кухня-гостиная (пом. 1), кухонный фронт	Стадия / Лист / Листов
Дизайнер	Кырлан А.С.			04.11.26		П / 42 / 71

Развёртка стены В: электроточки и выводы

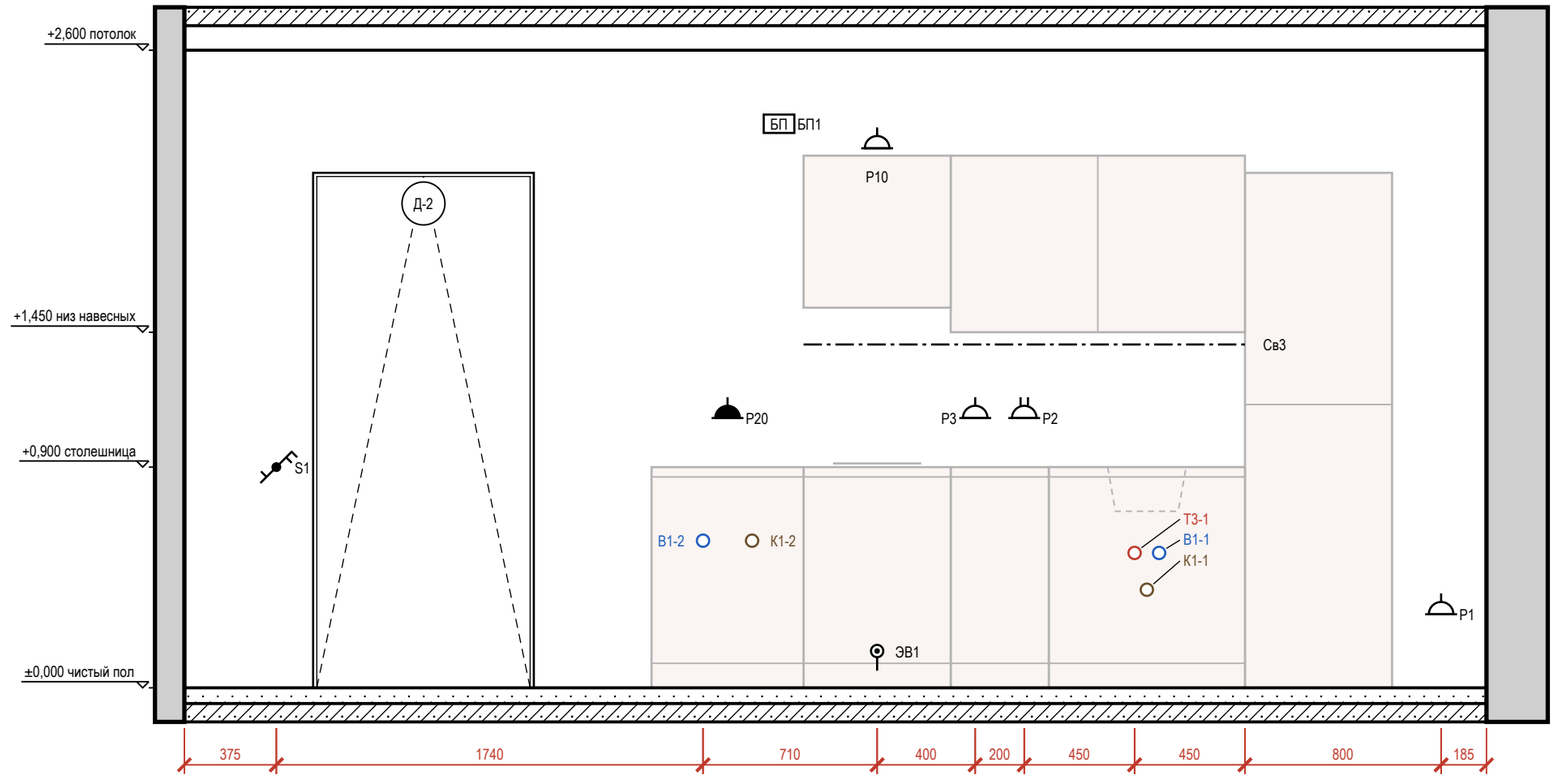


Таблица привязок электроточек и выводов

Марка	Назначение	От угла, мм	Н от пола, мм	Примечание
S1	выключатель	375	900	гр. 1
В1-2	холодная вода — стиральная машина	2115	600	кран машины
Р20	розетка: стиральная машина	2215	1100	гр. 6, IP44
К1-2	канализация — стиральная машина	2315	600	Ø40
БП1	блок питания LED	2425	2300	гр. 1
ЭВ1	вывод кабеля: варочная панель	2825	150	гр. 3
Р10	розетка: вытяжка (встроена в дно M_07)	2825	2200	гр. 2

Марка	Назначение	От угла, мм	Н от пола, мм	Примечание
Р3	розетка: рабочая зона	3225	1100	гр. 2
Р2	розетка: рабочая зона	3425	1100	рамка 2 поста, гр. 2
Т3-1	горячая вода — мойка кухонная	3875	550	межос. 100
К1-1	канализация — мойка кухонная	3925	400	Ø50
В1-1	холодная вода — мойка кухонная	3975	550	межос. 100
Св3	светильник настенный	4325	1400	гр. 1, лента 2525–4325 от угла
Р1	розетка: холодильник	5125	300	гр. 2

Условные обозначения

- розетка с заземляющим контактом; у знака — марка, ×N постов в рамке, гр. — группа щита, Н — высота оси, мм
- розетка влагозащищённая IP44
- вывод кабеля для подключения прибора (без розетки), марка ЭВ
- выключатель одноклавишный
- выключатель двухклавишный (флажков — по числу клавиш)
- выключатель с проходной или перекрёстной клавишей (обратный флажок); тип клавиши — в подписи
- светодиодная лента в профиле / в карнизе короба
- БП — блок питания LED, с доступом (люк от 100×100 мм)
- вывод В1 (код — в ведомости привязок)
- вывод Т3 (код — в ведомости привязок)
- вывод К1 (код — в ведомости привязок)
- привязки точек и выводов от угла и от пола, мм

Примечания

1. Вид «Привязки» стены В — электроточки и выводы ВК; архитектурная развёртка (мебель, отделка, проёмы, высоты) — на листе 42. Мебель и приборы — подложкой для ориентира; их марки и обозначения мебели, проёмов и стен — там же.
2. Привязки — в мм: по горизонтали от левого чистового угла стены до оси изделия, Н — от чистого пола до оси; все точки — в таблице привязок. Красная цепочка — привязки по осям; точки ближе 150 мм одна к другой в цепочку не дробятся — их привязки только в таблице.
3. У знака — марка электроточки (Р — розетка, S — выключатель, Св — светильник, ЭВ — вывод кабеля); условные обозначения и общие указания — лист 3.
4. Коды выводов ВК: В1 — холодная вода, Т3 — горячая вода, К1 — канализация; номер после дефиса — номер вывода на листе выводов сантехники.
5. Выводы кухонной техники — по утверждённому проекту кухни: привязки выводов даются от осей модулей гарнитура.

					Проект: Квартира 58 м² — М 1:25
	Лист	№ док.	Подпись	Дата	Привязки электроточек и выводов ВК, стена В. Кухня-гостиная (пом. 1)
Дизайнер	Кырлан А.С.			04.11.26	

Стадия	Лист	Листов
П	43	71

Развёртка стены А


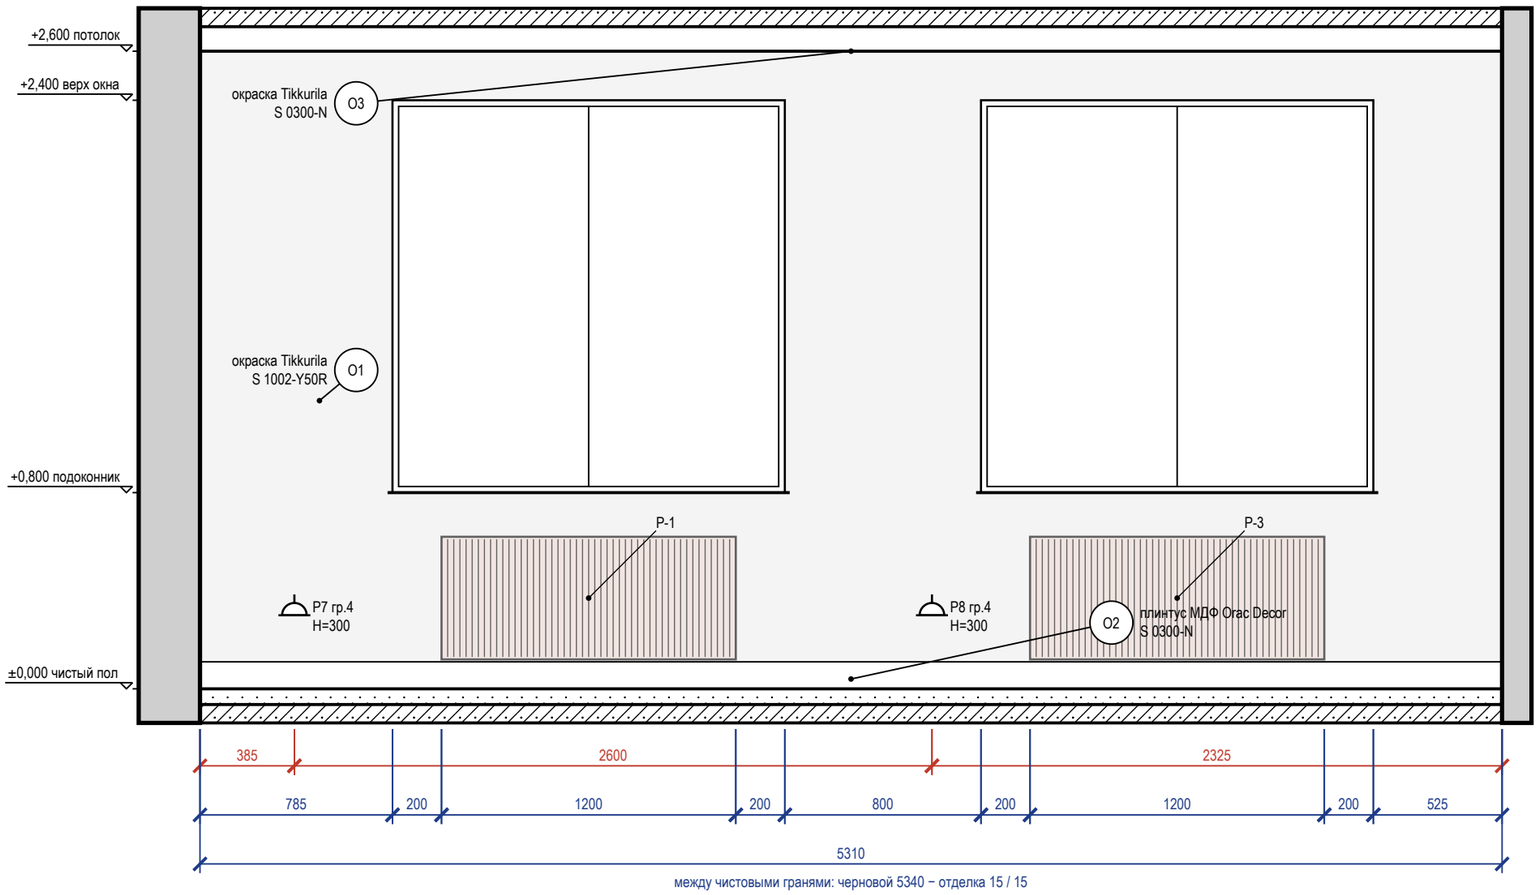


Схема развёрток (М 1:100)

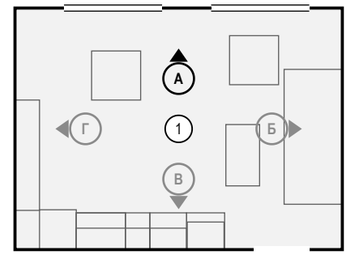

Ведомость отделки (на листе)

Марка	Поверхность	Материал, изделие	Цвет, код	Кол.
O1	стены	окраска, Tikkurila, шелковисто-матовая, подготовка Q3	NCS S 1002-Y50R	8,7 м²
O2	плинтус	плинтус МДФ, Orac Decor Luxxus, h 110 мм, SX184, шелковисто-матовая	NCS S 0300-N	5,3 м
O3	потолок	окраска, Tikkurila, глубокоматовая	NCS S 0300-N	21 м²

Примечания

1. Размеры — в мм от чистовых поверхностей стен; условные обозначения и общие указания — лист 3.
2. Потолок — у каждой стены свой, по плану потолков (ПТ2); ступени — зоной, кромка короба перед нишей — тонкой линией; в поле потолка: ПТ1 +2,550.

					Проект: Квартира 58 м² — М 1:25
	Лист	№ док.	Подпись	Дата	Развёртка стены А. Кухня-гостиная (пом. 1)
Дизайнер	Кырлан А.С.			04.11.26	Стадия: П; Лист: 44; Листов: 71

Развёртка стены Б


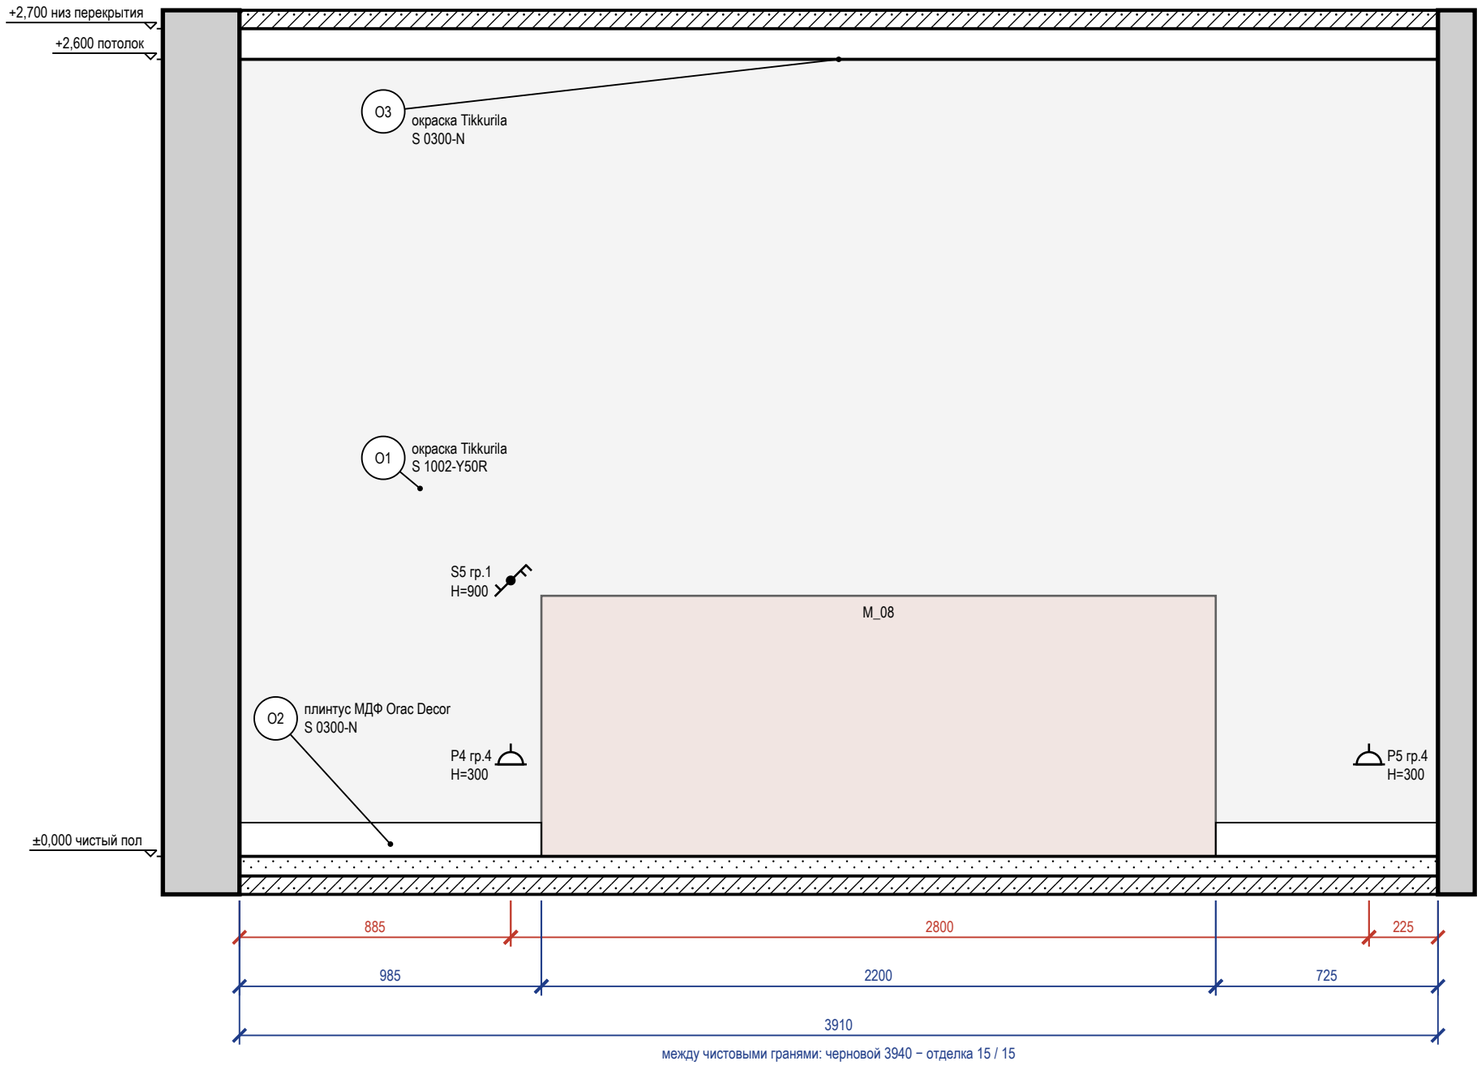


Схема развёрток (М 1:100)

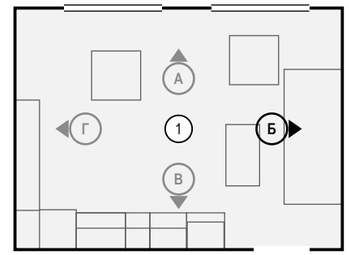

Ведомость отделки (на листе)

Марка	Поверхность	Материал, изделие	Цвет, код	Кол.
О1	стены	окраска, Tikkurila, шелковисто-матовая, подготовка Q3	NCS S 1002-Y50R	10,2 м²
О2	плинтус	плинтус МДФ, Orac Decor Luxxus, h 110 мм, SX184, шелковисто-матовая	NCS S 0300-N	1,7 м
О3	потолок	окраска, Tikkurila, глубокоматовая	NCS S 0300-N	21 м²

Примечания

1. Размеры — в мм от чистовых поверхностей стен; условные обозначения и общие указания — лист 3.
2. Потолок — у каждой стены свой, по плану потолков (ПТ2); ступени — зоной, кромка короба перед нишей — тонкой линией; в поле потолка: ПТ1 +2,550.

	Лист	№ док.	Подпись	Дата
Дизайнер	Кырлан А.С.			04.11.26

Проект: Квартира 58 м² — **М 1:20**

Развёртка стены Б. Кухня-гостиная (пом. 1)

Стадия	Лист	Листов
П	45	71

Развёртка стены Г


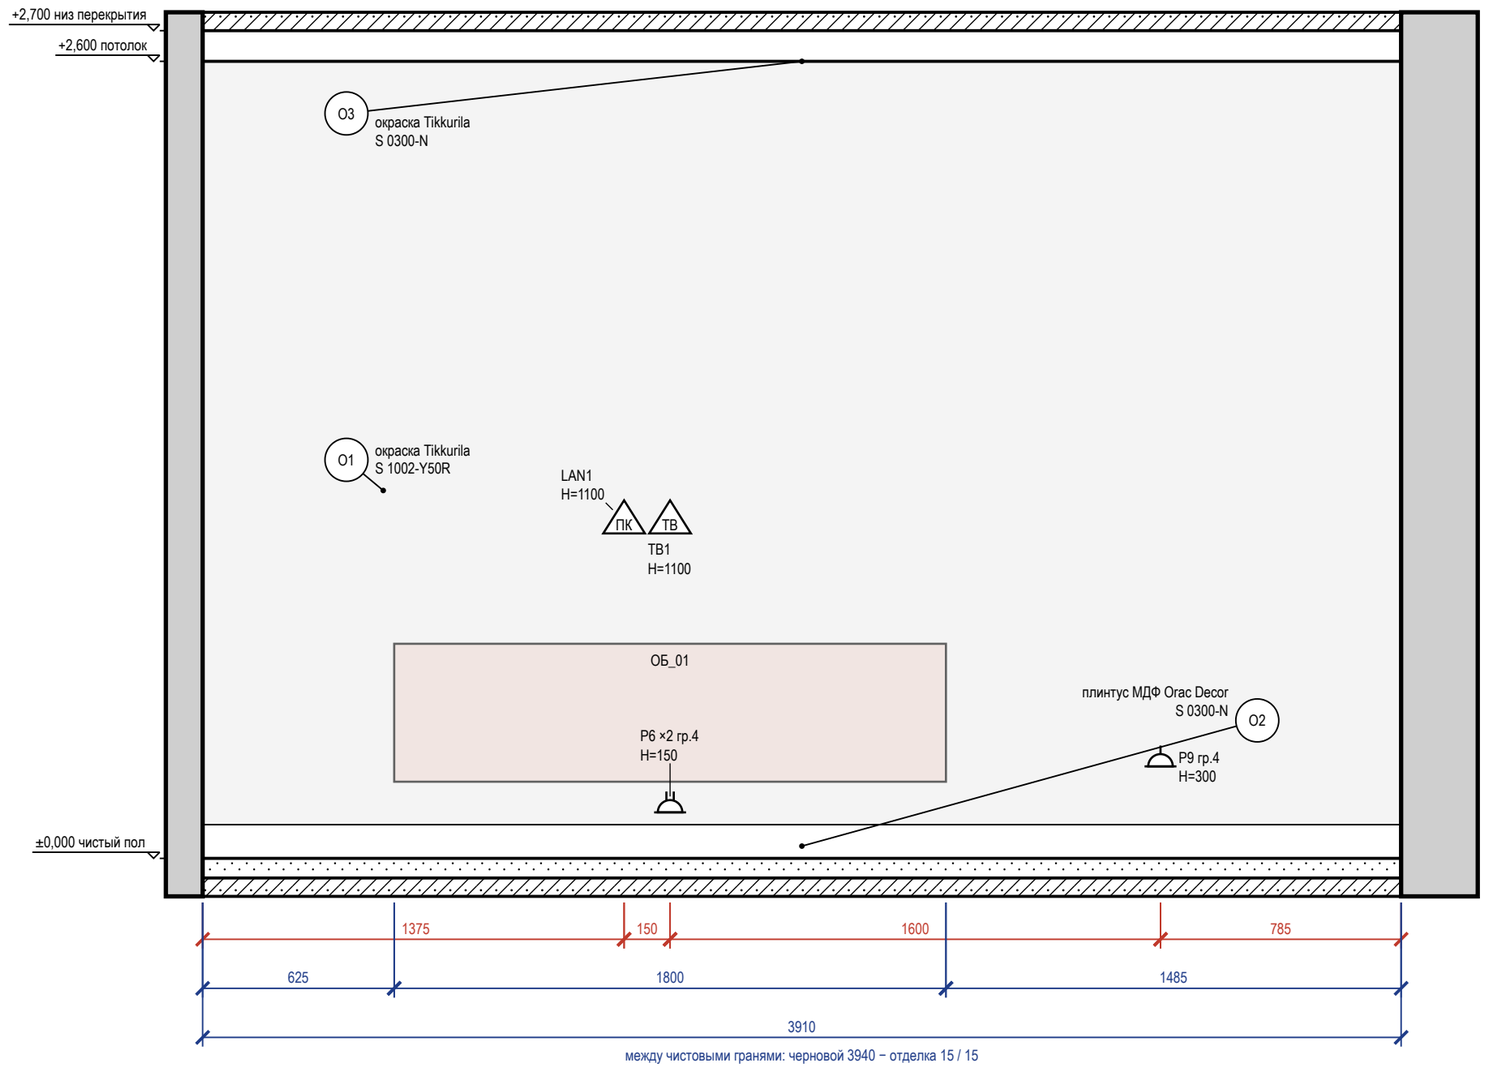


Схема развёрток (М 1:100)

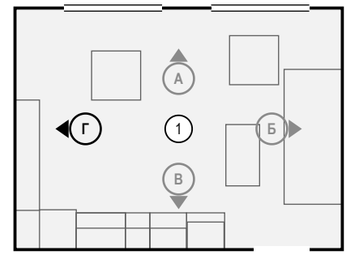

Ведомость отделки (на листе)

Марка	Поверхность	Материал, изделие	Цвет, код	Кол.
О1	стены	окраска, Tikkurila, шелковисто-матовая, подготовка Q3	NCS S 1002-Y50R	10,2 м²
О2	плинтус	плинтус МДФ, Orac Decor Luxxus, h 110 мм, SX184, шелковисто-матовая	NCS S 0300-N	3,9 м
О3	потолок	окраска, Tikkurila, глубокоматовая	NCS S 0300-N	21 м²

Примечания

1. Размеры — в мм от чистовых поверхностей стен; условные обозначения и общие указания — лист 3.
2. Потолок — у каждой стены свой, по плану потолков (ПТ2); ступени — зоной, кромка короба перед нишей — тонкой линией; в поле потолка: ПТ1 +2,550.

					Проект: Квартира 58 м² — М 1:20
	Лист	№ док.	Подпись	Дата	Развёртка стены Г. Кухня-гостиная (пом. 1)
Дизайнер	Кырлан А.С.			04.11.26	Стадия: П; Лист: 46; Листов: 71

Развёртка стены А


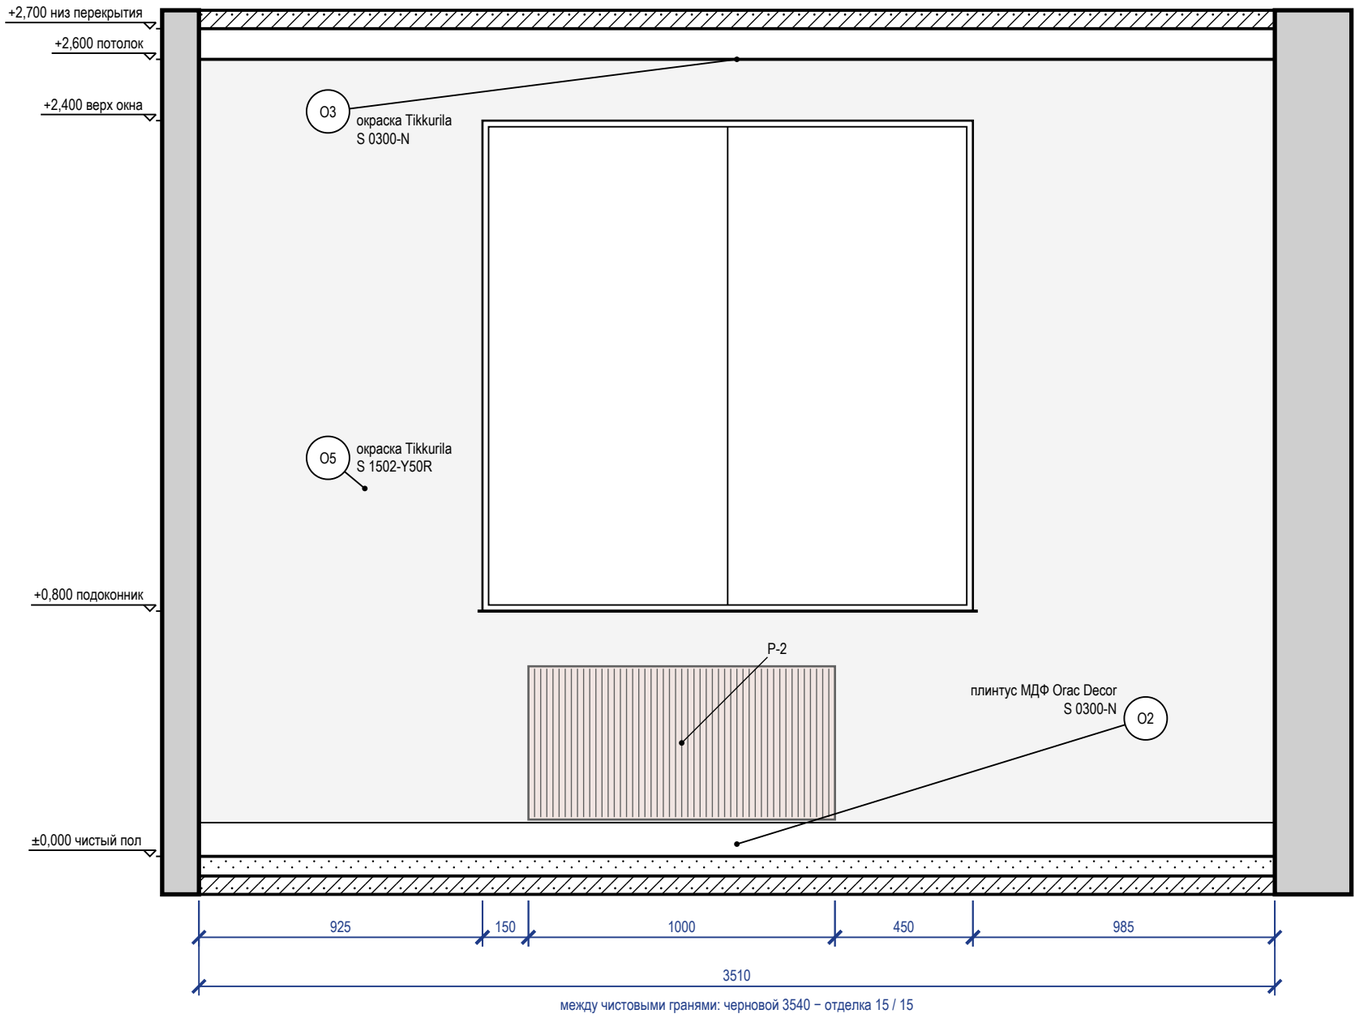


Схема развёрток (М 1:100)

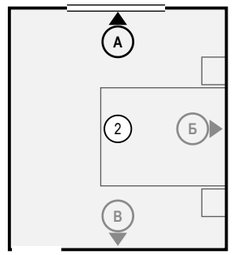

Ведомость отделки (на листе)

Марка	Поверхность	Материал, изделие	Цвет, код	Кол.
О2	плинтус	плинтус МДФ, Orac Decor Luxxus, h 110 мм, SX184, шелковисто-матовая	NCS S 0300-N	3,5 м
О3	потолок	окраска, Tikkurila, глубокоматовая	NCS S 0300-N	13,9 м²
О5	стены	окраска, Tikkurila, глубокоматовая, подготовка Q3	NCS S 1502-Y50R	6,6 м²

Примечания

1. Размеры — в мм от чистовых поверхностей стен; условные обозначения и общие указания — лист 3.
2. Потолок — у каждой стены свой, по плану потолков (ПТ2); ступени — зоной, кромка короба перед нишей — тонкой линией; в поле потолка: ПТ1 +2,550.

					Проект: Квартира 58 м² — М 1:20
	Лист	№ док.	Подпись	Дата	
Дизайнер	Кырлан А.С.			04.11.26	Развёртка стены А. Спальня (пом. 2)
					Стадия: П; Лист: 47; Листов: 71

Развёртка стены Б


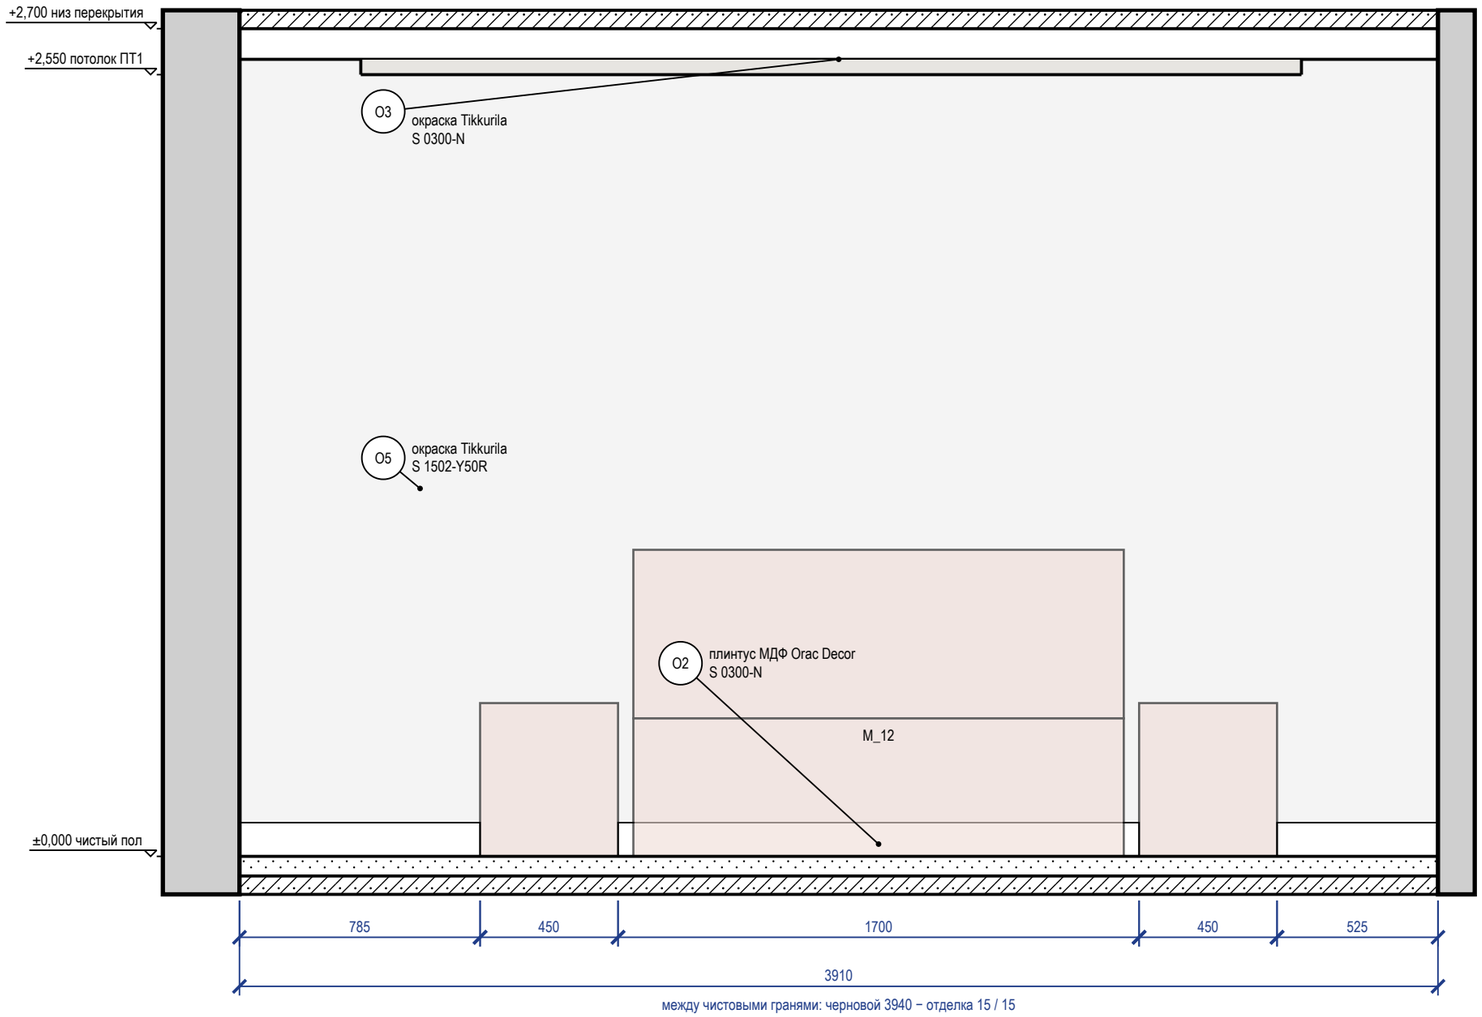


Схема развёрток (М 1:100)

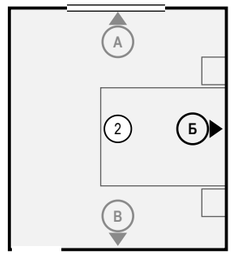

Ведомость отделки (на листе)

Марка	Поверхность	Материал, изделие	Цвет, код	Кол.
О2	плинтус	плинтус МДФ, Orac Decor Luxxus, h 110 мм, SX184, шелковисто-матовая	NCS S 0300-N	3 м
О3	потолок	окраска, Tikkurila, глубокоматовая	NCS S 0300-N	13,9 м²
О5	стены	окраска, Tikkurila, глубокоматовая, подготовка Q3	NCS S 1502-Y50R	10,2 м²

Примечания

1. Размеры — в мм от чистовых поверхностей стен; условные обозначения и общие указания — лист 3.
2. Стена Б показана двумя видами: здесь — архитектурная развёртка (мебель, отделка, проёмы, высоты), электроточки и выводы ВК с привязками и таблицей — на листе 49 («Привязки»).
3. Потолок — у каждой стены свой, по плану потолков (ПТ2, ПТ1); ступени — зоной, кромка короба перед нишей — тонкой линией.

	Лист	№ док.	Подпись	Дата
Дизайнер	Кырлан А.С.			04.11.26

Проект: Квартира 58 м² — **М 1:20**

Развёртка стены Б. Спальня (пом. 2)

Стадия	Лист	Листов
П	48	71

Развёртка стены Б: электроточки и выводы

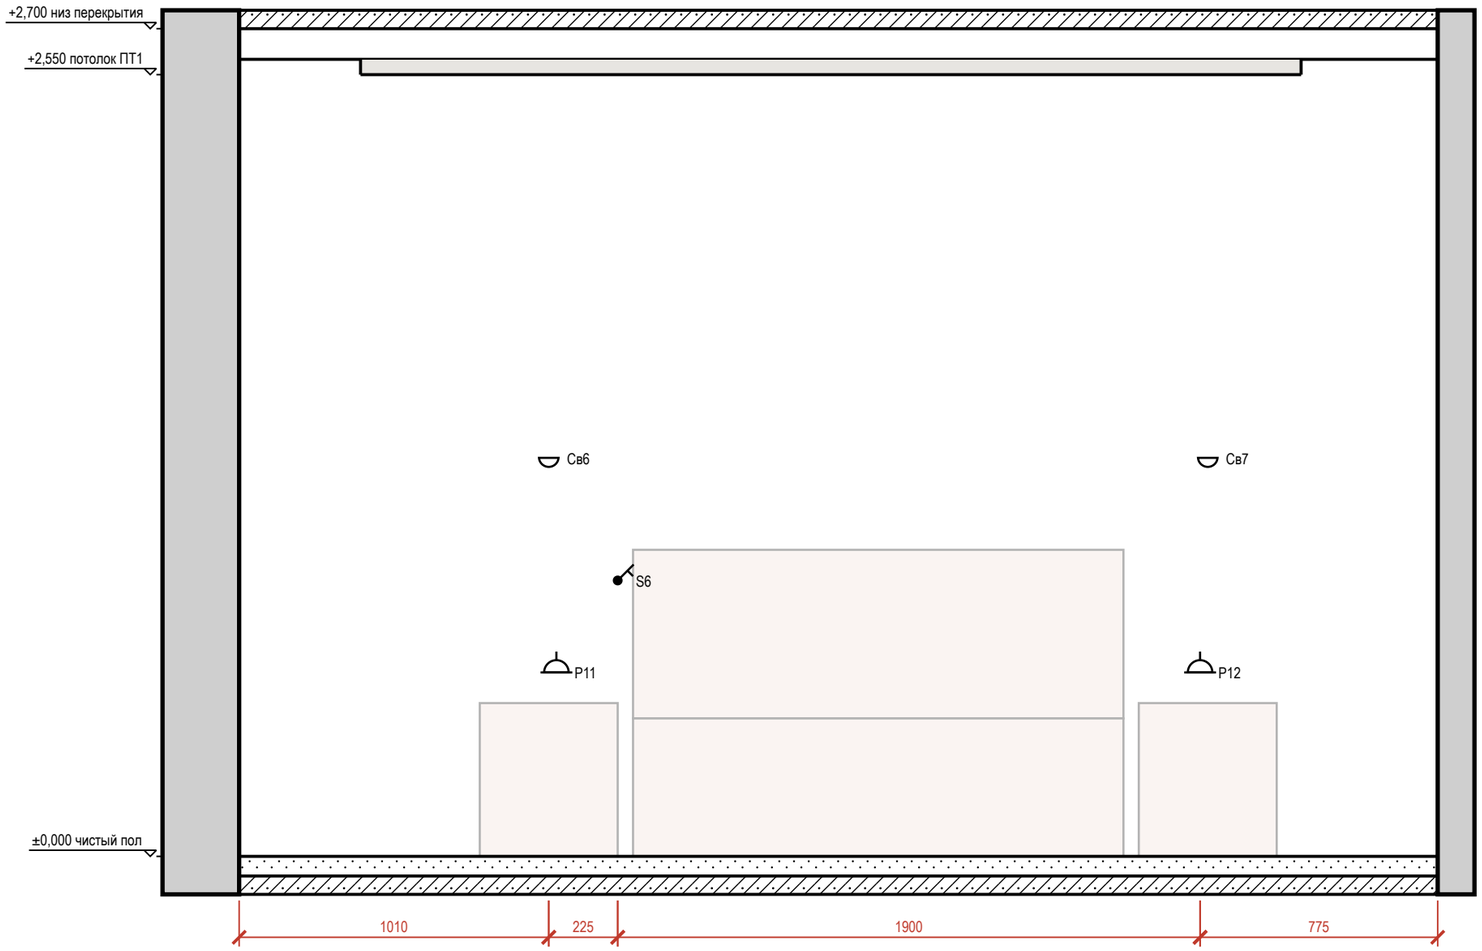



Таблица привязок электроточек и выводов

Марка	Назначение	От угла, мм	Н от пола, мм	Примечание
Св6	светильник настенный	1010	1300	гр. 1
Р11	розетка	1035	600	гр. 4
S6	выключатель	1235	900	гр. 1
Р12	розетка	3135	600	гр. 4
Св7	светильник настенный	3160	1300	гр. 1

Условные обозначения

- розетка с заземляющим контактом; у знака — марка, ×N постов в рамке, гр. — группа щита, Н — высота оси, мм
- выключатель одноклавишный
- светильник настенный (бра), Н — высота оси
- привязки точек и выводов от угла и от пола, мм
- марка развёртки: буква стены, стрелка — взгляд

Схема развёрток (М 1:50)

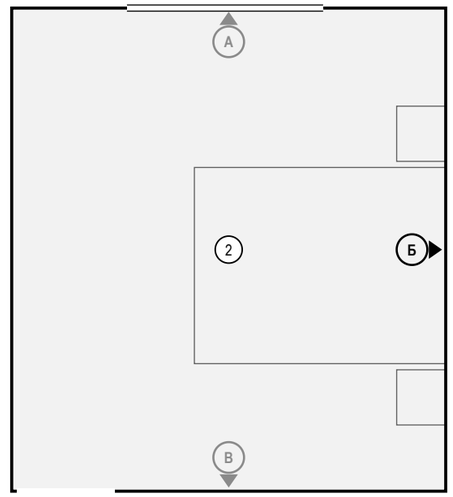

Примечания

1. Вид «Привязки» стены Б — электроточки и выводы ВК; архитектурная развёртка (мебель, отделка, проёмы, высоты) — на листе 48. Мебель и приборы — подложкой для ориентира; их марки и обозначения мебели, проёмов и стен — там же.
2. Привязки — в мм: по горизонтали от левого чистового угла стены до оси изделия, Н — от чистого пола до оси; все точки — в таблице привязок. Красная цепочка — привязки по осям; точки ближе 120 мм одна к другой в цепочку не дробятся — их привязки только в таблице.
3. У знака — марка электроточки (Р — розетка, S — выключатель, Св — светильник, ЭВ — вывод кабеля); условные обозначения и общие указания — лист 3.

					Проект: Квартира 58 м² — М 1:20
	Лист	№ док.	Подпись	Дата	Привязки электроточек, стена Б. Спальня (пом. 2)
Дизайнер	Кырлан А.С.			04.11.26	Стадия: П; Лист: 49; Листов: 71

Развёртка стены В


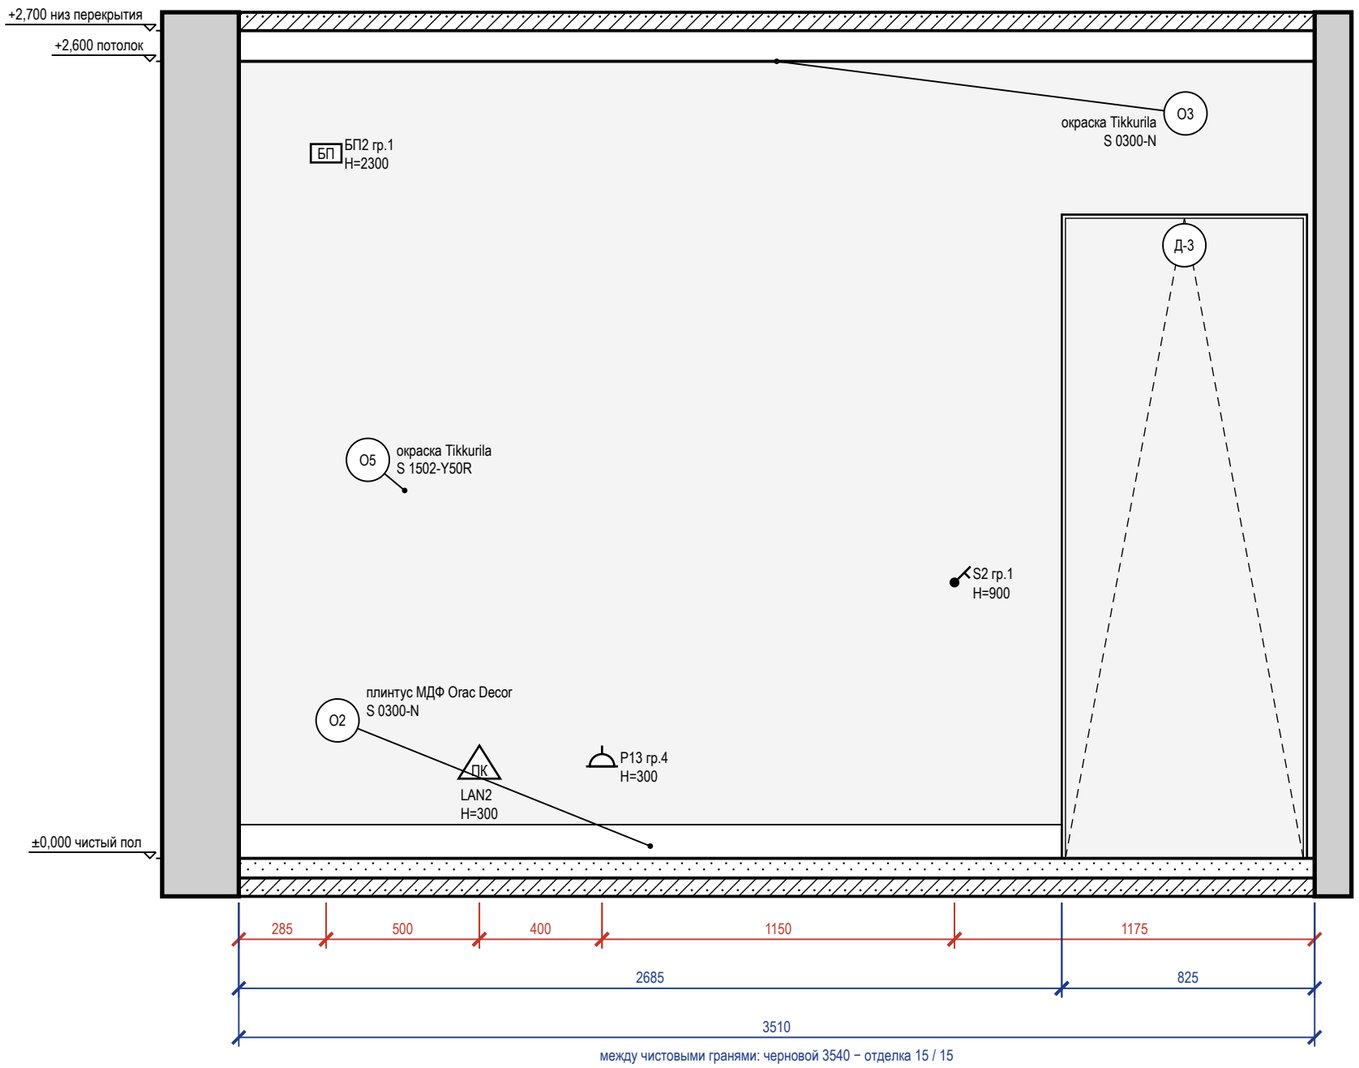


Схема развёрток (М 1:100)

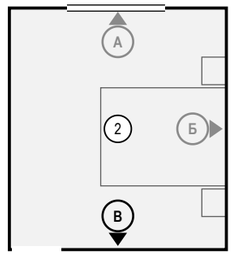


Ведомость отделки (на листе)

Марка	Поверхность	Материал, изделие	Цвет, код	Кол.
О2	плинтус	плинтус МДФ, Orac Decor Luxxus, h 110 мм, SX184, шелковисто-матовая	NCS S 0300-N	2,7 м
О3	потолок	окраска, Tikkurila, глубокоматовая	NCS S 0300-N	13,9 м²
О5	стены	окраска, Tikkurila, глубокоматовая, подготовка Q3	NCS S 1502-Y50R	7,4 м²

5 **Плинтус МДФ 110×16 мм у окрашенной стены по доске (ламинату) (М 1:10)**

Узел 5 — лист С5

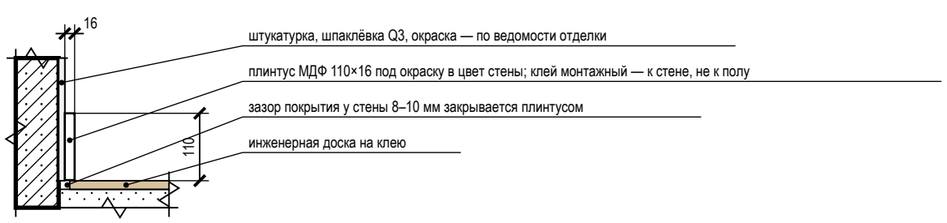


Примечания

1. Размеры — в мм от чистовых поверхностей стен; условные обозначения и общие указания — лист 3.
2. Двери скрытого монтажа — полотно в плоскости стены, отделка стены по полотну, плинтус прерывается у короба (узел — на листе узлов).
3. Потолок — у каждой стены свой, по плану потолков (ПТ2); ступени — зоной, кромка короба перед нишей — тонкой линией; в поле потолка: ПТ1 +2,550.


					Проект: Квартира 58 м²	М 1:20
	Лист	№ док.	Подпись	Дата	Развёртка стены В. Спальня (пом. 2)	Стадия / Лист / Листов
Дизайнер	Кырлан А.С.			04.11.26		П / 50 / 71

Развёртка стены А

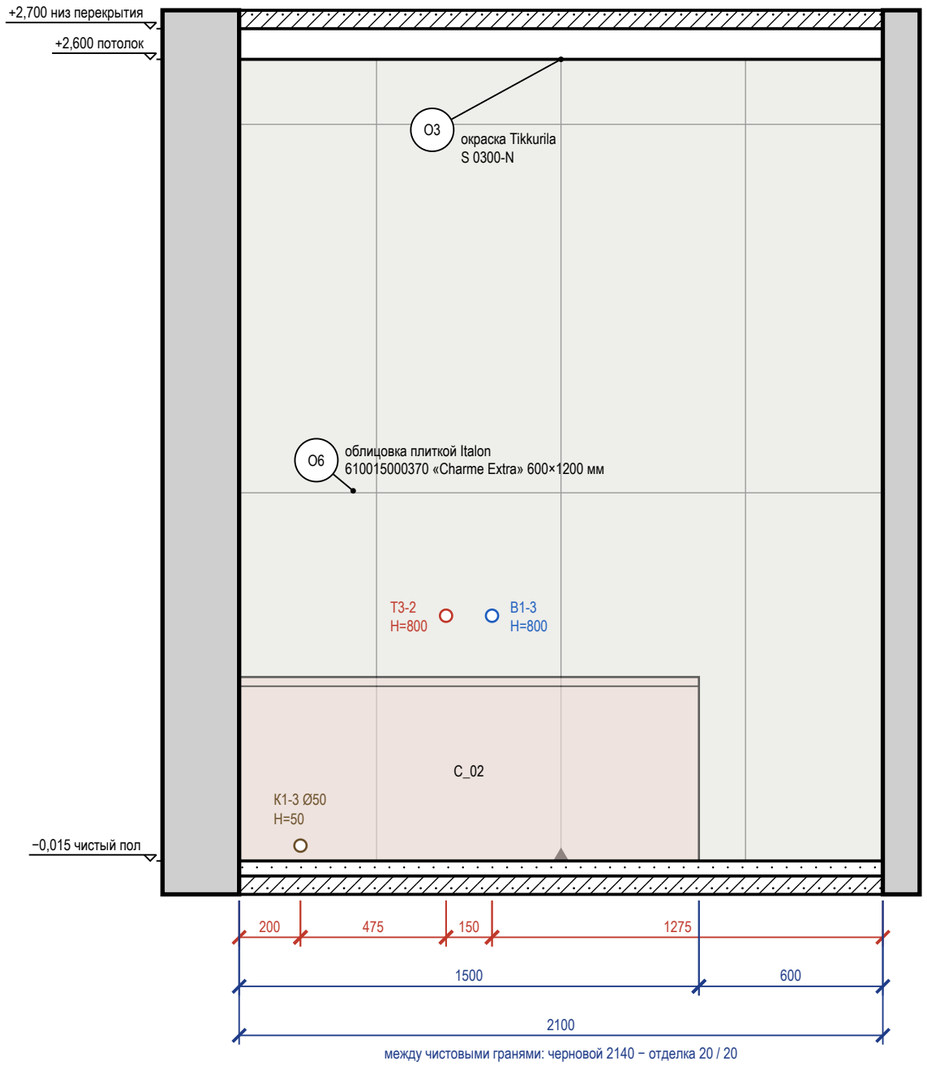


между чистовыми гранями: черновой 2140 − отделка 20 / 20

Развёртка стены Б

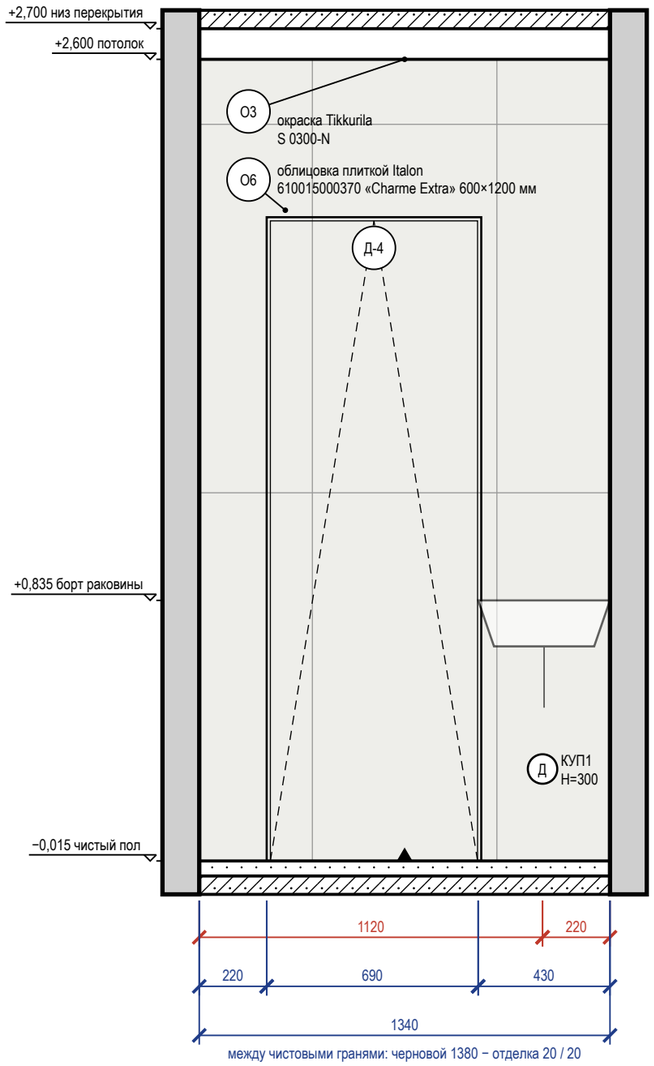

между чистовыми гранями: черновой 1380 − отделка 20 / 20

Схема развёрток (М 1:100)

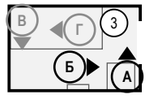


Ведомость отделки (на листе)

Марка	Поверхность	Материал, изделие	Цвет, код	Кол.
О3	потолок	окраска, Tikkurila, глубокоматовая	NCS S 0300-N	3 м²
О6	стены	облицовка плиткой, Italon Charme Extra, 600×1200 мм, 610015000370	Italon 610015000370 «Charme Extra»	7,5 м²

1 **Порог 15 мм: мокрая зона — смежное помещение (М 1:10)**

Узел 1 — лист С5

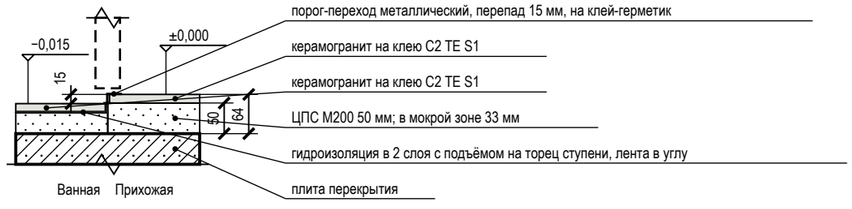


Примечания

1. Размеры — в мм от чистовых поверхностей стен; условные обозначения и общие указания — лист 3.
2. Облицовка — по сетке швов, раскладка от оси стены (треугольник у пола); подрезки — по листу раскладки плитки.
3. Гидроизоляция в 2 слоя, заход на стены 200 мм; над ванной — до 2000 и 300 мм за борт — до облицовки, с актом скрытых работ и тестом проливом (узел — на листе узлов).
4. Двери скрытого монтажа — полотно в плоскости стены, отделка стены по полотну, плинтус прерывается у короба (узел — на листе узлов).

					Проект: Квартира 58 м²	М 1:20
	Лист	№ док.	Подпись	Дата		
Дизайнер	Кырлан А.С.			04.11.26	Развёртки стен А, Б. Ванная (пом. 3)	
					Стадия: П	Лист: 51 / Листов: 71

Развёртка стены В

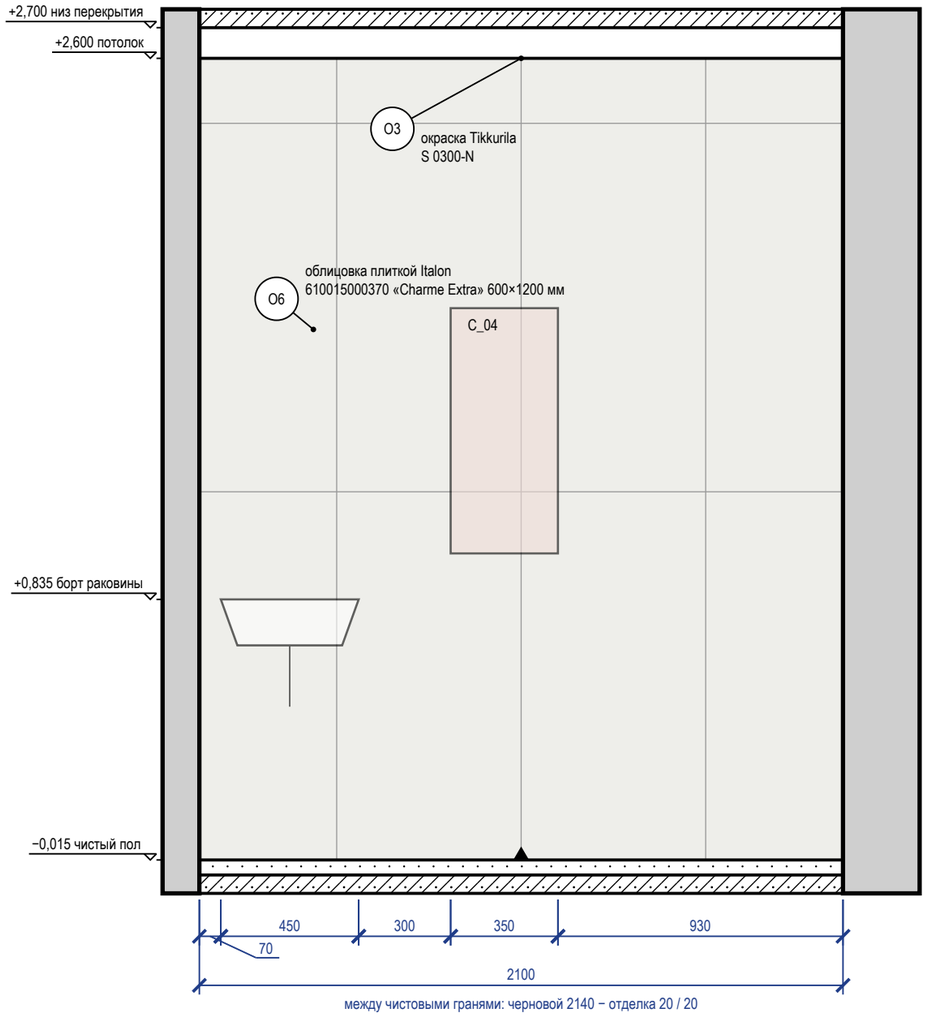

Развёртка стены Г


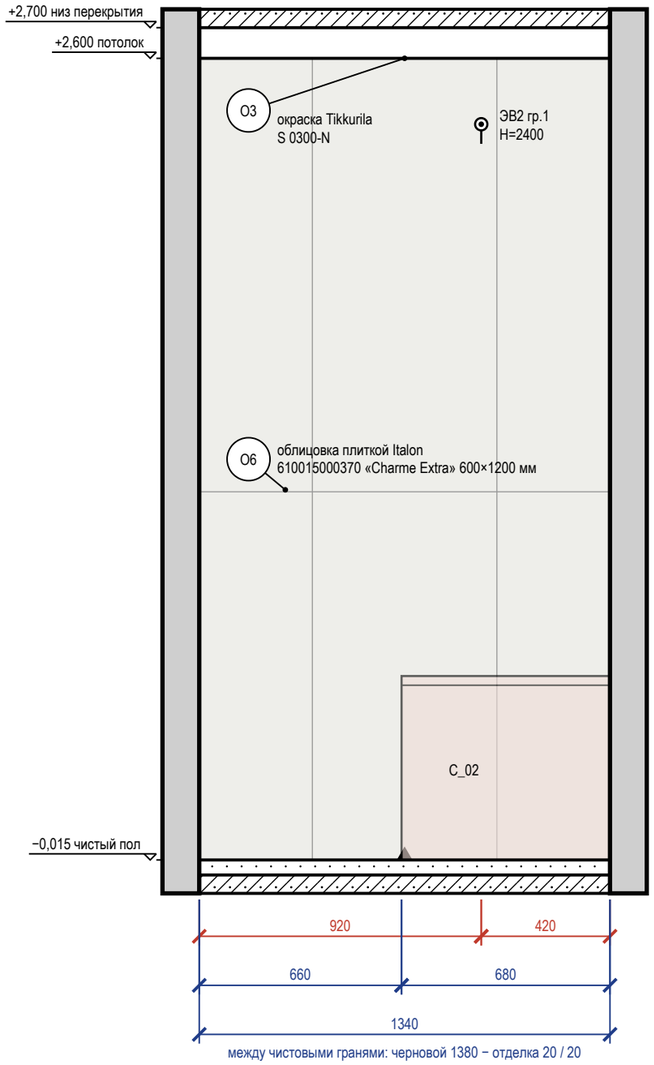


Схема развёрток (М 1:100)

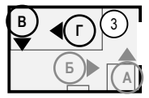


Ведомость отделки (на листе)

Марка	Поверхность	Материал, изделие	Цвет, код	Кол.
О3	потолок	окраска, Tikkurila, глубокоматовая	NCS S 0300-N	3 м²
О6	стены	облицовка плиткой, Italon Charme Extra, 600×1200 мм, 610015000370	Italon 610015000370 «Charme Extra»	9 м²

3 **Короб стояков К1-1 с люком и звукоизоляцией (М 1:20)**

Узел 3 — лист С5

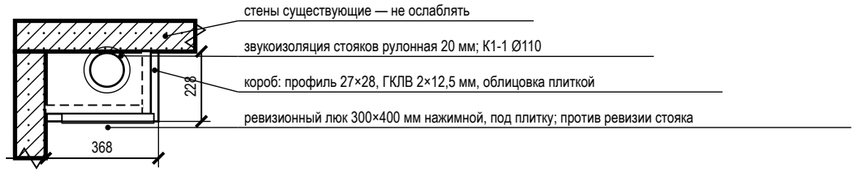

Примечания

1. Размеры — в мм от чистовых поверхностей стен; условные обозначения и общие указания — лист 3.
2. Стена В показана двумя видами: здесь — архитектурная развёртка (мебель, отделка, проёмы, высоты), электроточки и выводы ВК с привязками и таблицей — на листе 53 («Привязки»).
3. Облицовка — по сетке швов, раскладка от оси стены (треугольник у пола); подрезки — по листу раскладки плитки.
4. Гидроизоляция в 2 слоя, заход на стены 200 мм; над ванной — до 2000 и 300 мм за борт — до облицовки, с актом скрытых работ и тестом проливом (узел — на листе узлов).

					Проект: Квартира 58 м²	М 1:20
	Лист	№ док.	Подпись	Дата		
Дизайнер	Кырлан А.С.			04.11.26	Развёртки стен В, Г. Ванная (пом. 3)	Стадия: П; Лист: 52; Листов: 71

Развёртка стены В: электроточки и выводы

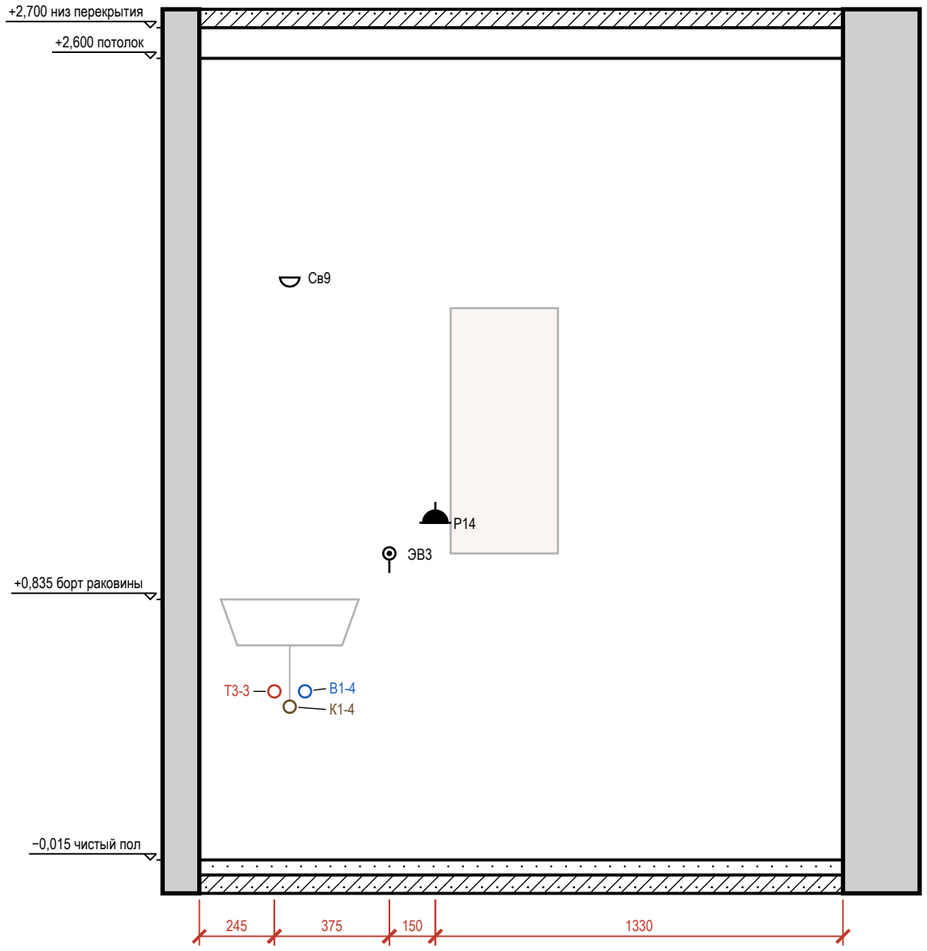



Таблица привязок электроточек и выводов

Марка	Назначение	От угла, мм	Н от пола, мм	Примечание
Т3-3	горячая вода — умывальник	245	550	межос. 100
К1-4	канализация — умывальник	295	500	Ø50
Св9	светильник настенный	295	1900	гр. 1
В1-4	холодная вода — умывальник	345	550	межос. 100
ЭВ3	вывод кабеля: полотенцесушитель	620	1000	гр. 5
Р14	розетка: фен	770	1100	гр. 5, IP44

Условные обозначения

- розетка влагозащищённая IP44
- вывод кабеля для подключения прибора (без розетки), марка ЭВ
- светильник настенный (бра), Н — высота оси
- вывод В1 (код — в ведомости привязок)
- вывод Т3 (код — в ведомости привязок)
- вывод К1 (код — в ведомости привязок)
- привязки точек и выводов от угла и от пола, мм
- марка развёртки: буква стены, стрелка — взгляд

Схема развёрток (М 1:50)

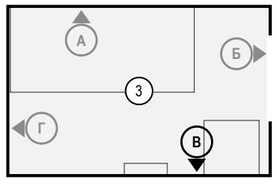


Примечания

1. Вид «Привязки» стены В — электроточки и выводы ВК; архитектурная развёртка (мебель, отделка, проёмы, высоты) — на листе 52. Мебель и приборы — подложкой для ориентира; их марки и обозначения мебели, проёмов и стен — там же.
2. Привязки — в мм: по горизонтали от левого чистового угла стены до оси изделия, Н — от чистого пола до оси; все точки — в таблице привязок. Красная цепочка — привязки по осям; точки ближе 120 мм одна к другой в цепочку не дробятся — их привязки только в таблице.
3. У знака — марка электроточки (Р — розетка, S — выключатель, Св — светильник, ЭВ — вывод кабеля); условные обозначения и общие указания — лист 3.
4. Коды выводов ВК: В1 — холодная вода, Т3 — горячая вода, К1 — канализация; номер после дефиса — номер вывода на листе выводов сантехники.

					Проект: Квартира 58 м² — М 1:20
	Лист	№ док.	Подпись	Дата	Привязки электроточек и выводов ВК, стена В. Ванная (пом. 3)
Дизайнер	Кырлан А.С.			04.11.26	


Стадия	Лист	Листов
П	53	71

Развёртка стены А

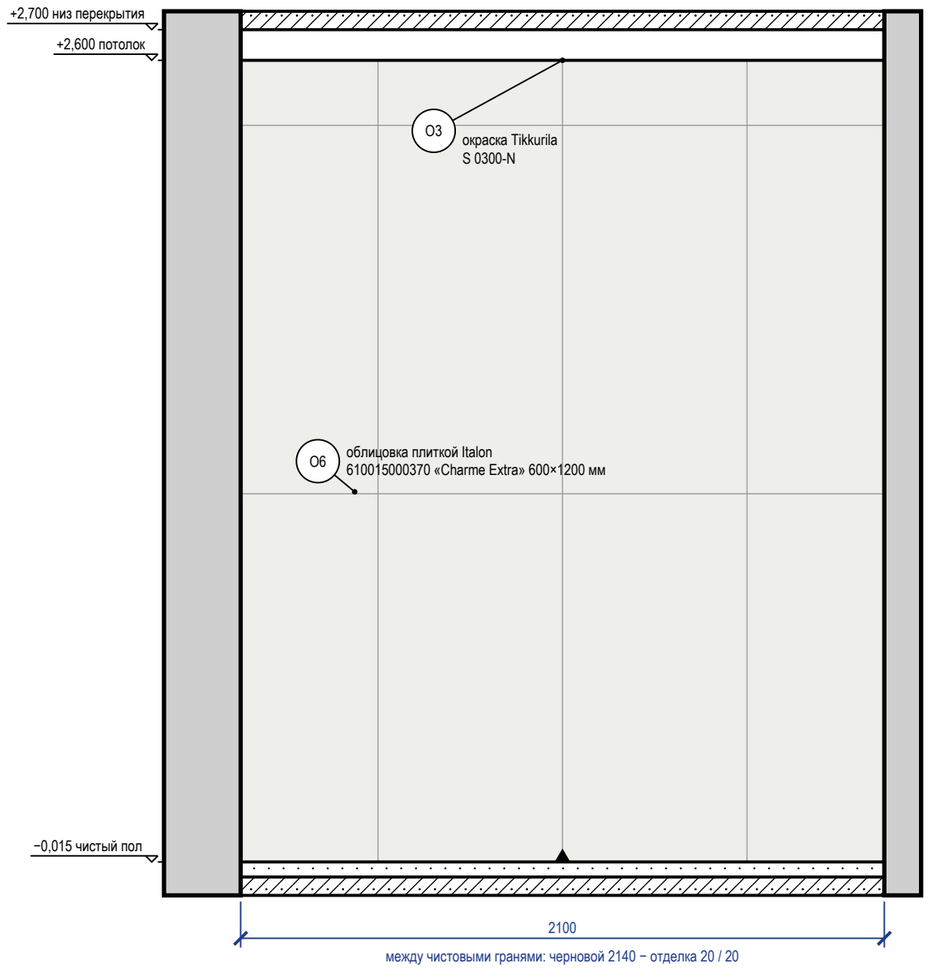


между чистовыми гранями: черновой 2140 − отделка 20 / 20

Развёртка стены Б

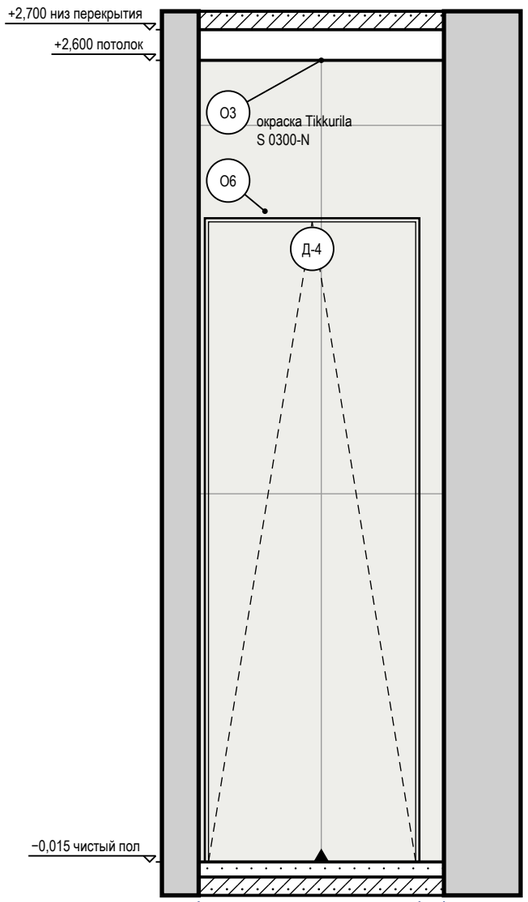

между чистовыми гранями: черновой 840 − отделка 20 / 20

Схема развёрток (М 1:100)

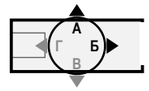

Ведомость отделки (на листе)


Марка	Поверхность	Материал, изделие	Цвет, код	Кол.
О3	потолок	окраска, Tikkurila, глубокоматовая	NCS S 0300-N	1,8 м²
О6	стены	облицовка плиткой, Italon Charme Extra, 600×1200 мм, 610015000370	Italon 610015000370 «Charme Extra»	6,1 м²

Примечания

1. Размеры — в мм от чистовых поверхностей стен; условные обозначения и общие указания — лист 3.
2. Облицовка — по сетке швов, раскладка от оси стены (треугольник у пола); подрезки — по листу раскладки плитки.
3. Гидроизоляция в 2 слоя, заход на стены 200 мм — до облицовки, с актом скрытых работ и тестом проливом (узел — на листе узлов).
4. Двери скрытого монтажа — полотно в плоскости стены, отделка стены по полотну, плинтус прерывается у короба (узел — на листе узлов).


					Проект: Квартира 58 м²	М 1:20
	Лист	№ док.	Подпись	Дата		
Дизайнер	Кырлан А.С.			04.11.26	Развёртки стен А, Б. Санузел (пом. 4)	
					Стадия: П	Лист: 54 / Листов: 71

Развёртка стены В

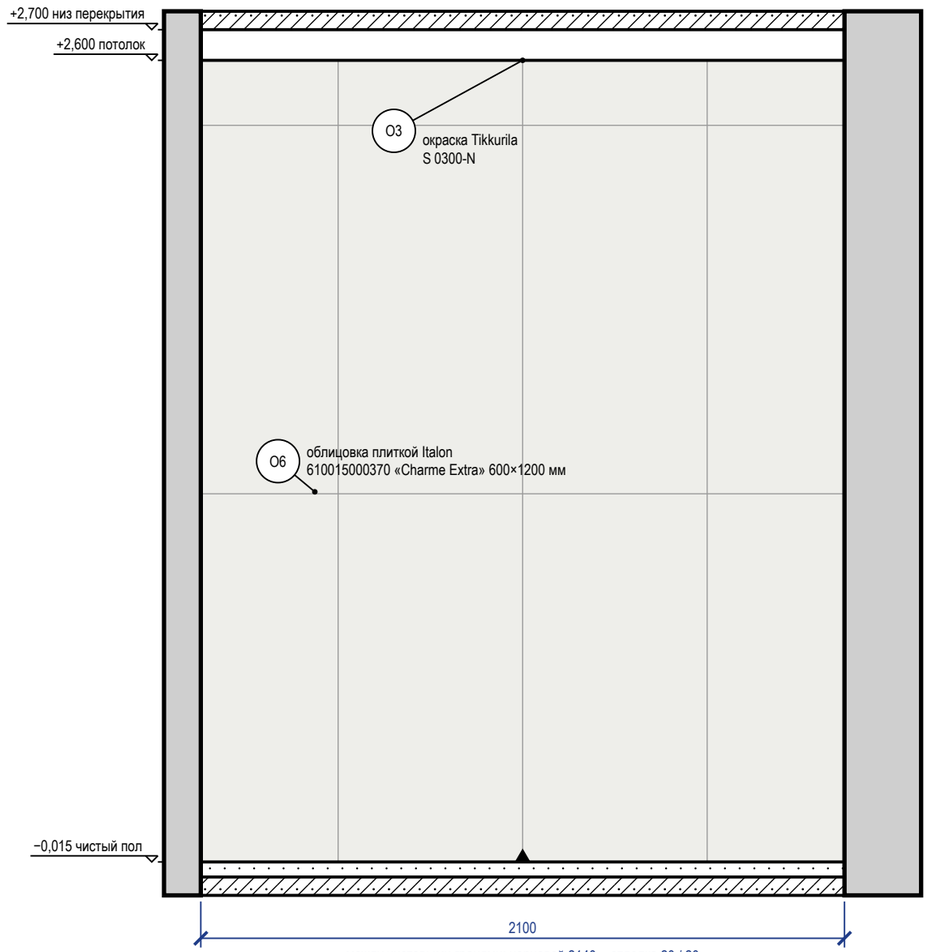


между чистовыми гранями: черновой 2140 − отделка 20 / 20

Развёртка стены Г

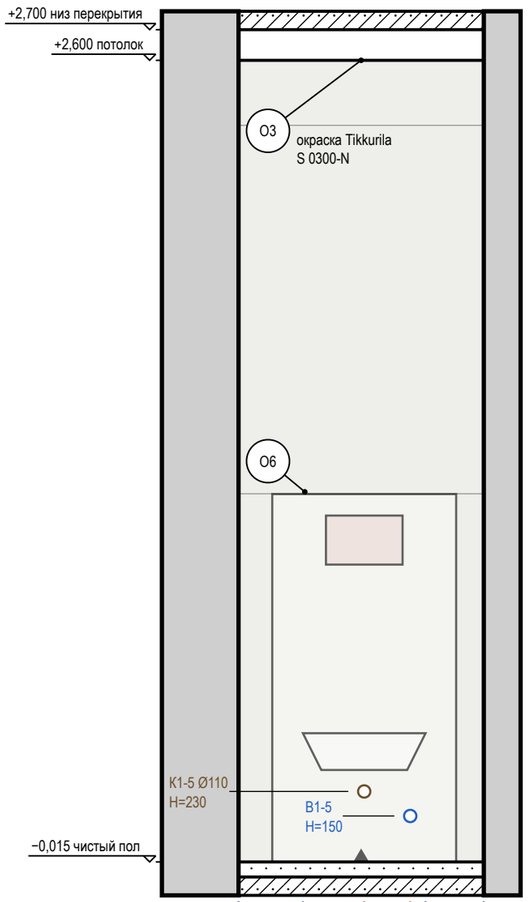

между чистовыми гранями: черновой 840 − отделка 20 / 20

Схема развёрток (М 1:100)

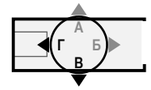

Ведомость отделки (на листе)

Марка	Поверхность	Материал, изделие	Цвет, код	Кол.
О3	потолок	окраска, Tikkurila, глубокоматовая	NCS S 0300-N	1,8 м²
О6	стены	облицовка плиткой, Italon Charme Extra, 600×1200 мм, 610015000370	Italon 610015000370 «Charme Extra»	7,6 м²

Примечания

1. Размеры — в мм от чистовых поверхностей стен; условные обозначения и общие указания — лист 3.
2. Схема мебели, приборов и декора не является технической документацией для производства мебели; габариты — по паспортам изделий.
3. Облицовка — по сетке швов, раскладка от оси стены (треугольник у пола); подрезки — по листу раскладки плитки.
4. Гидроизоляция в 2 слоя, заход на стены 200 мм — до облицовки, с актом скрытых работ и тестом проливом (узел — на листе узлов).

					Проект: Квартира 58 м²	М 1:20
	Лист	№ док.	Подпись	Дата		
Дизайнер	Кырлан А.С.			04.11.26	Развёртки стен В, Г. Санузел (пом. 4)	Стадия: П; Лист: 55; Листов: 71

Развёртка стены А


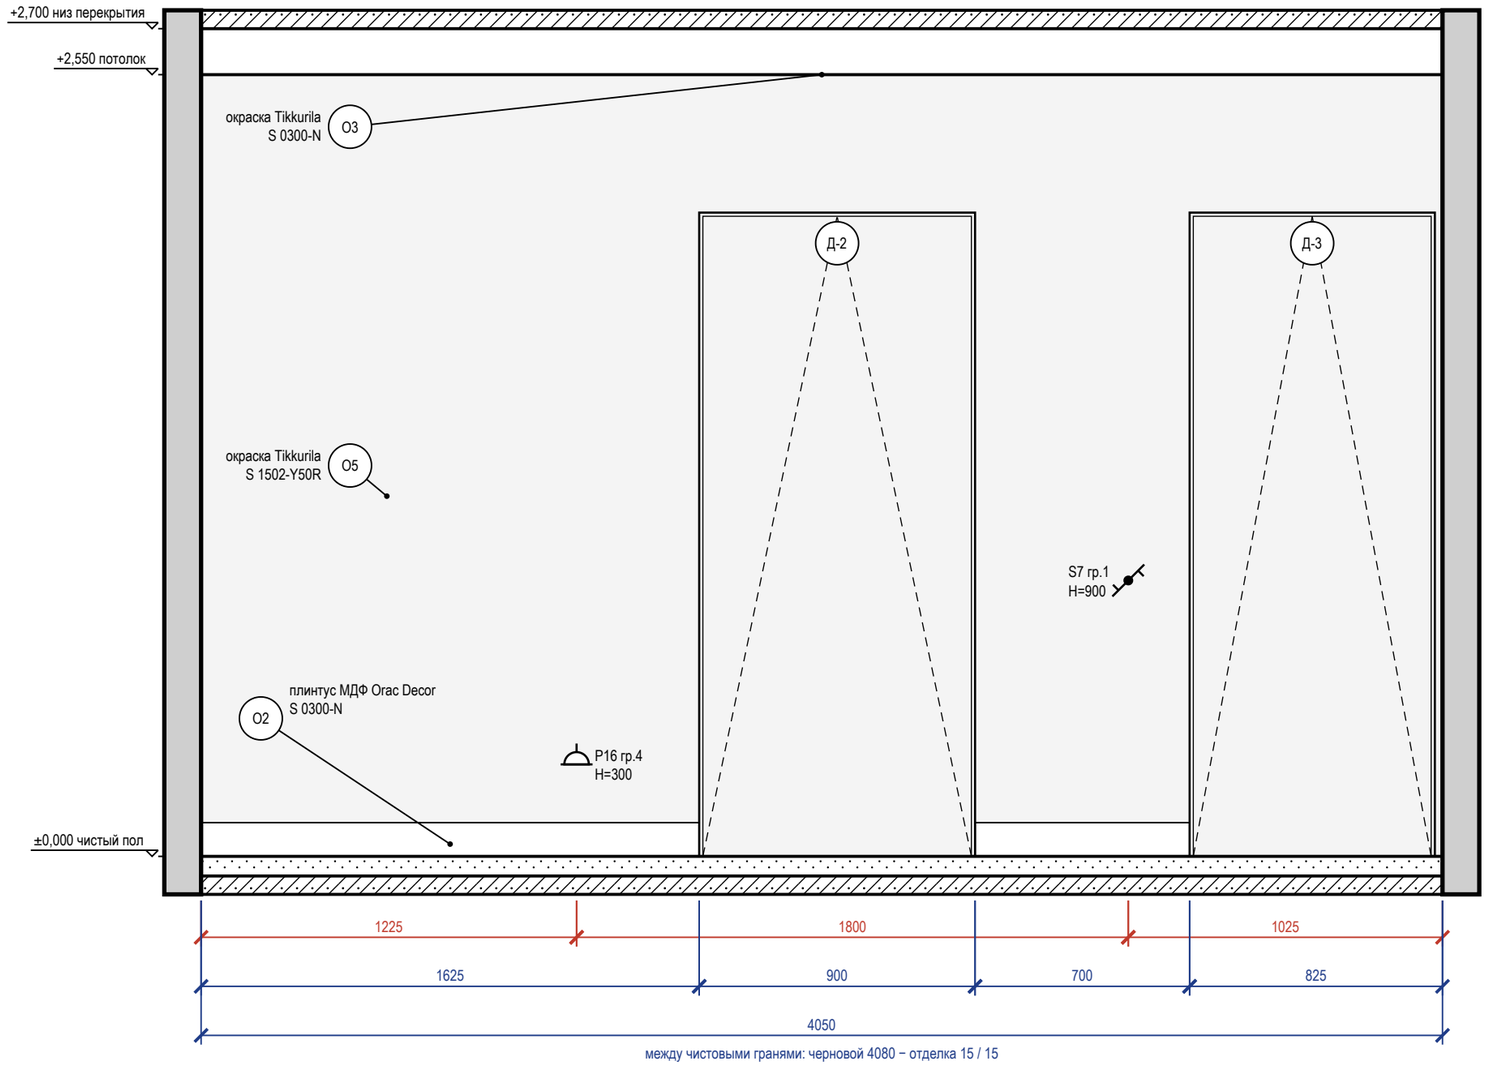


Схема развёрток (М 1:100)

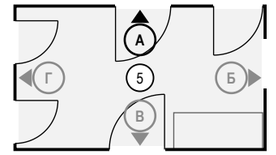

Ведомость отделки (на листе)


Марка	Поверхность	Материал, изделие	Цвет, код	Кол.
О2	плинтус	плинтус МДФ, Orac Decor Luxxus, h 110 мм, SX184, шелковисто-матовая	NCS S 0300-N	2,3 м
О3	потолок	окраска, Tikkurila, глубокоматовая	NCS S 0300-N	9,6 м²
О5	стены	окраска, Tikkurila, шелковисто-матовая, подготовка Q3	NCS S 1502-Y50R	6,8 м²

Примечания

1. Размеры — в мм от чистовых поверхностей стен; условные обозначения и общие указания — лист 3.
2. Двери скрытого монтажа — полотно в плоскости стены, отделка стены по полотну, плинтус прерывается у короба (узел — на листе узлов).
3. Потолок — у каждой стены свой, по плану потолков (ПТ1); ступени — зоной, кромка короба перед нишей — тонкой линией; в поле потолка: ПТ2 +2,600.


					Проект: Квартира 58 м²	М 1:20
	Лист	№ док.	Подпись	Дата	Развёртка стены А. Прихожая (пом. 5)	Стадия / Лист / Листов
Дизайнер	Кырлан А.С.			04.11.26		П / 56 / 71

Развёртка стены Б

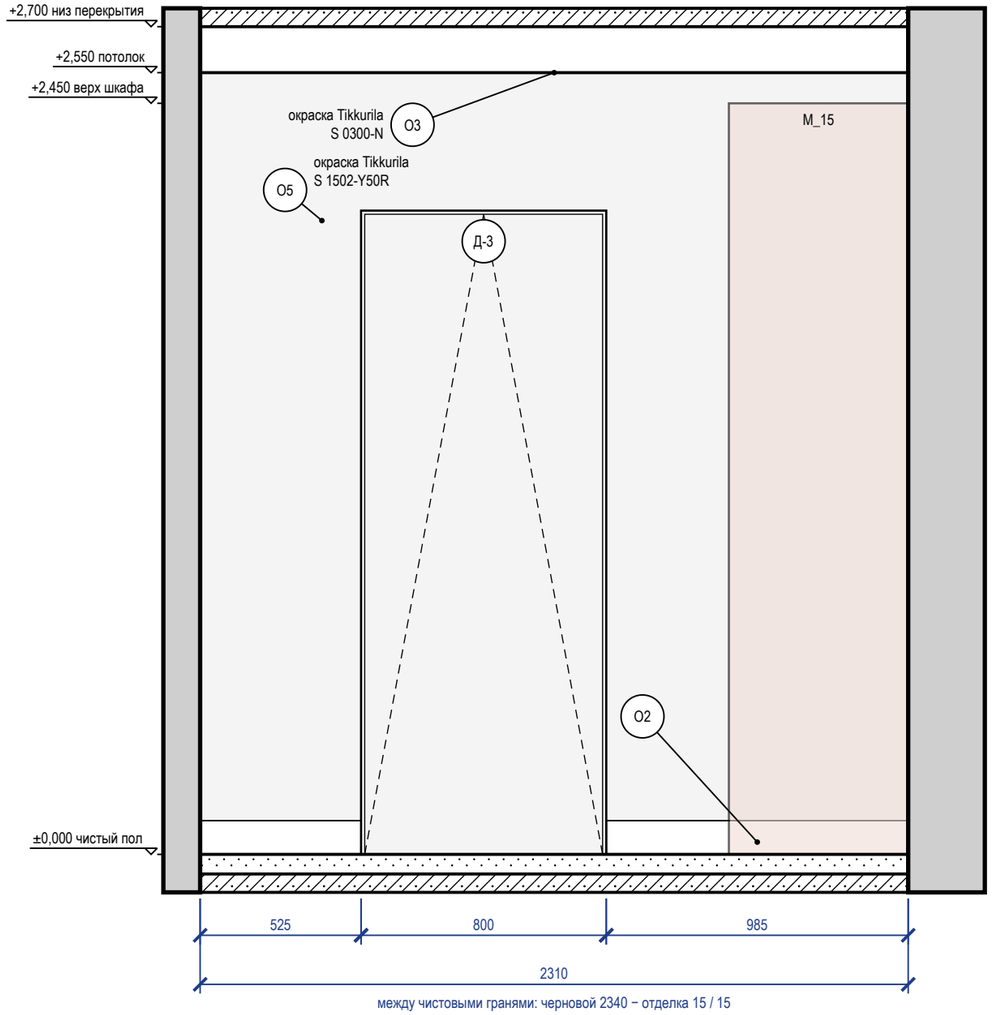


между чистовыми гранями: черновой 2340 − отделка 15 / 15

Развёртка стены Г

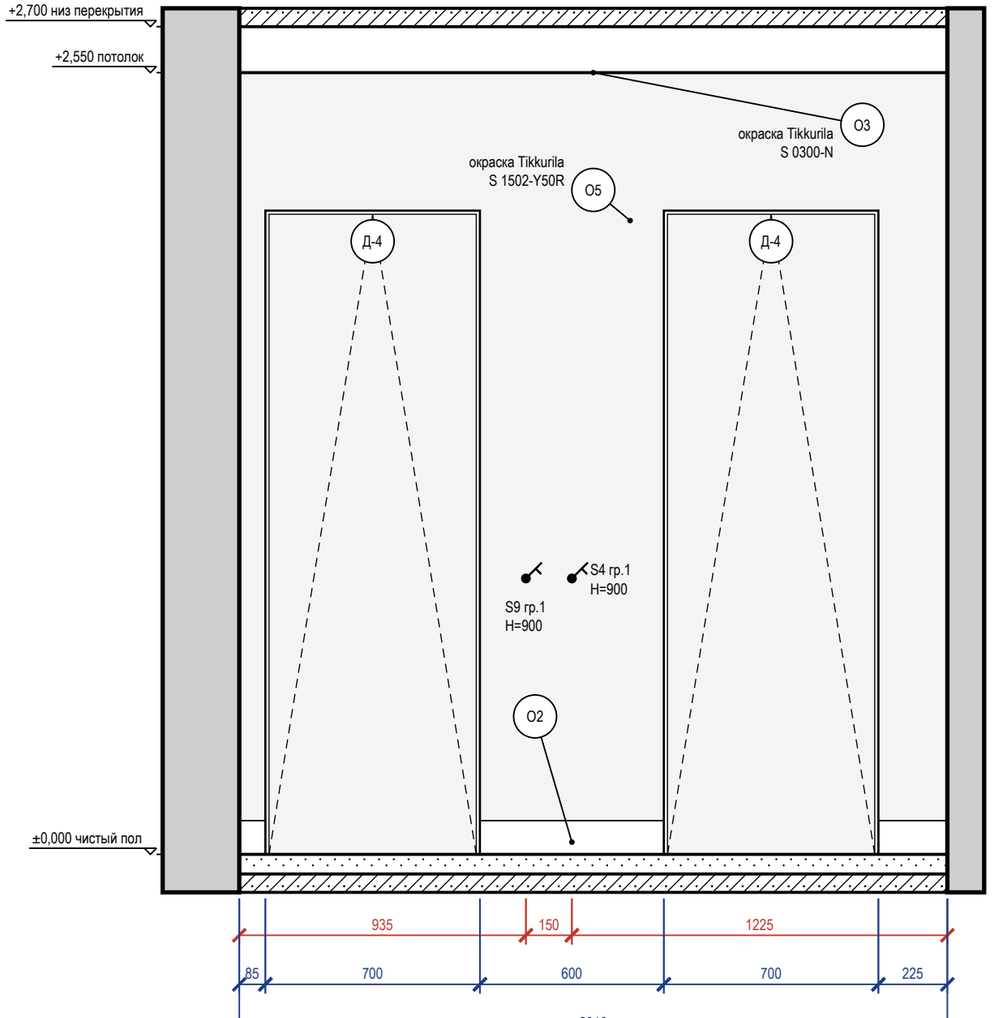

между чистовыми гранями: черновой 2340 − отделка 15 / 15

Схема развёрток (М 1:100)

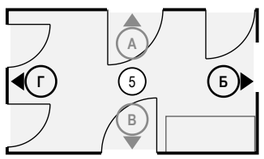

Ведомость отделки (на листе)

Марка	Поверхность	Материал, изделие	Цвет, код	Кол.
О2	плинтус	плинтус МДФ, Orac Decor Luxxus, h 110 мм, SX184, шелковисто-матовая	NCS S 0300-N	2,4 м
О3	потолок	окраска, Tikkurila, глубокоматовая	NCS S 0300-N	9,6 м²
О5	стены	окраска, Tikkurila, шелковисто-матовая, подготовка Q3	NCS S 1502-Y50R	7,2 м²

Примечания

1. Размеры — в мм от чистовых поверхностей стен; условные обозначения и общие указания — лист 3.
2. Двери скрытого монтажа — полотно в плоскости стены, отделка стены по полотну, плинтус прерывается у короба (узел — на листе узлов).
3. Потолок — у каждой стены свой, по плану потолков (ПТ1); ступени — зоной, кромка короба перед нишей — тонкой линией; в поле потолка: ПТ2 +2,600.

					Проект: Квартира 58 м² — М 1:20
	Лист	№ док.	Подпись	Дата	Развёртки стен Б, Г. Прихожая (пом. 5)
Дизайнер	Кырлан А.С.			04.11.26	Стадия: П; Лист: 57; Листов: 71

выпуск 04.11.2026 № e0dc2f2b59 · стр. 57 из 71

Развёртка стены В


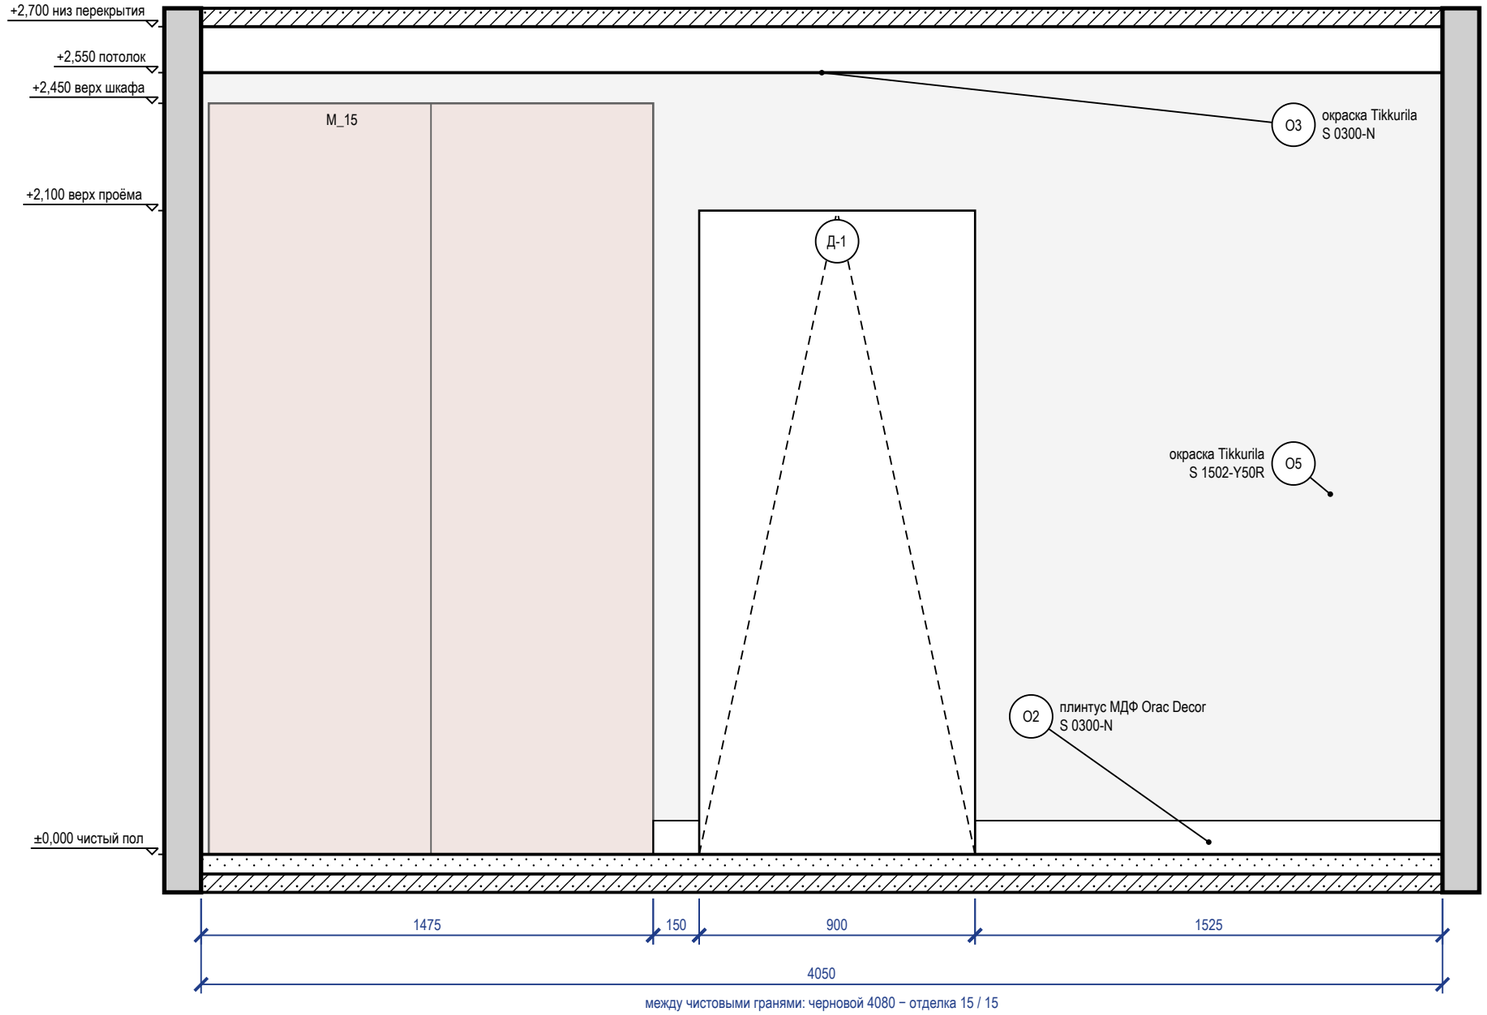


Схема развёрток (М 1:100)

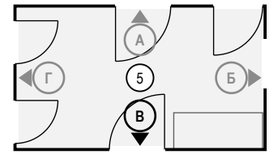


Ведомость отделки (на листе)

Марка	Поверхность	Материал, изделие	Цвет, код	Кол.
О2	плинтус	плинтус МДФ, Orac Decor Luxxus, h 110 мм, SX184, шелковисто-матовая	NCS S 0300-N	1,7 м
О3	потолок	окраска, Tikkurila, глубокоматовая	NCS S 0300-N	9,6 м²
О5	стены	окраска, Tikkurila, шелковисто-матовая, подготовка Q3	NCS S 1502-Y50R	8,4 м²

6 **Плинтус МДФ 110×16 мм у окрашенной стены по керамограниту (плитке) (М 1:10)**

Узел 6 — лист С5

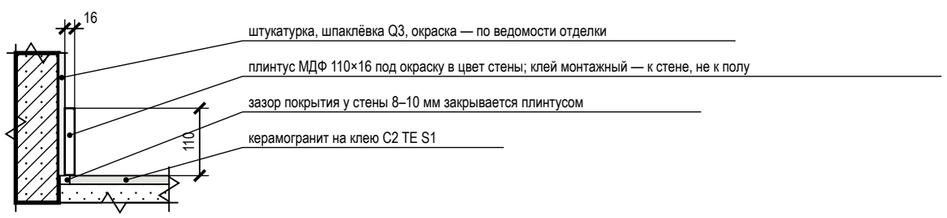

Примечания

1. Размеры — в мм от чистовых поверхностей стен; условные обозначения и общие указания — лист 3.
2. Стена В показана двумя видами: здесь — архитектурная развёртка (мебель, отделка, проёмы, высоты), электроточки и выводы ВК с привязками и таблицей — на листе 59 («Привязки»).
3. Потолок — у каждой стены свой, по плану потолков (ПТ1); ступени — зоной, кромка короба перед нишей — тонкой линией; в поле потолка: ПТ2 +2,600.

					Проект: Квартира 58 м² — М 1:20
	Лист	№ док.	Подпись	Дата	Развёртка стены В. Прихожая (пом. 5)
Дизайнер	Кырлан А.С.			04.11.26	Стадия: П; Лист: 58; Листов: 71

Развёртка стены В: электроточки и выводы

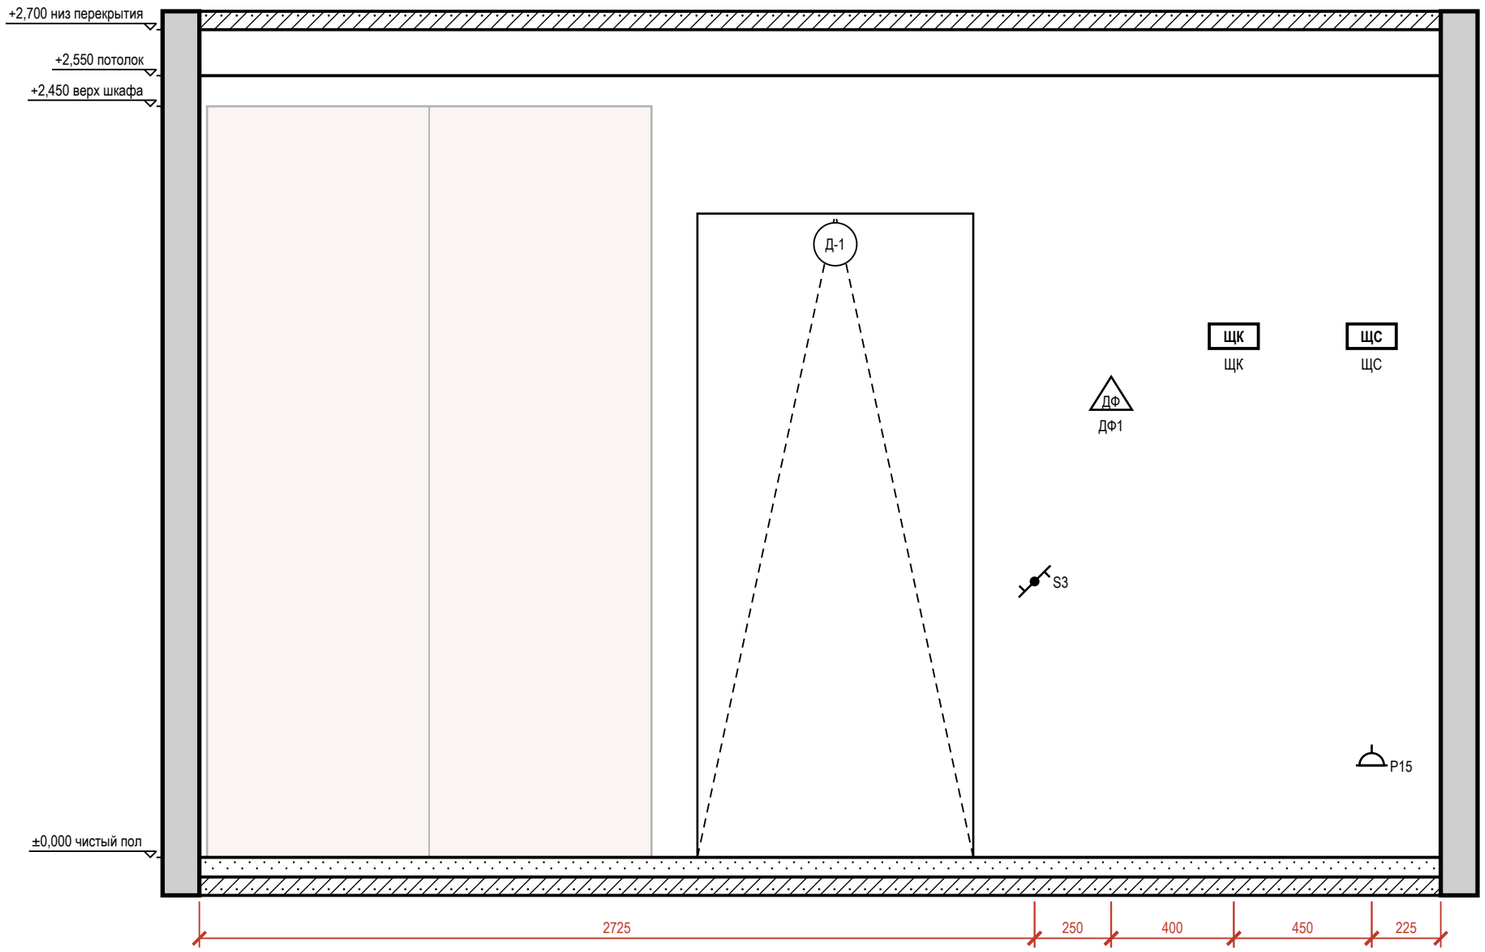



Таблица привязок электроточек и выводов

Марка	Назначение	От угла, мм	Н от пола, мм	Примечание
S3	выключатель	2725	900	гр. 1
ДФ1	домофон: трубка домофона	2975	1500	
ЩК	щит	3375	1700	
P15	розетка: питание ЩС (роутер, ИБП)	3825	300	гр. 4
ЩС	щит: щит слаботочный: ввод провайдера, роутер	3825	1700	

Условные обозначения

- розетка с заземляющим контактом; у знака — марка, ×N постов в рамке, гр. — группа щита, Н — высота оси, мм
- выключатель одноклавишный
- выключатель с проходной или перекрёстной клавишей (обратный флажок); тип клавиши — в подписи
- ДФ — трубка или монитор домофона
- ЩК — щит квартирный
- привязки точек и выводов от угла и от пола, мм
- А — марка развёртки: буква стены, стрелка — взгляд

Схема развёрток (М 1:50)

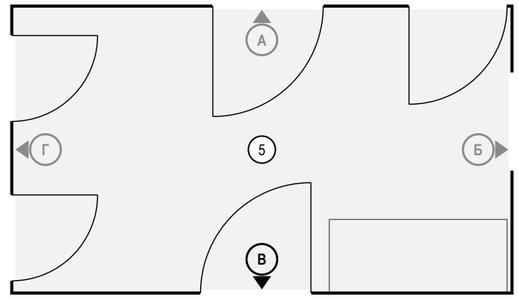


Примечания

1. Вид «Привязки» стены В — электроточки и выводы ВК; архитектурная развёртка (мебель, отделка, проёмы, высоты) — на листе 58. Мебель и приборы — подложкой для ориентира; их марки и обозначения мебели, проёмов и стен — там же.
2. Привязки — в мм: по горизонтали от левого чистового угла стены до оси изделия, Н — от чистого пола до оси; все точки — в таблице привязок. Красная цепочка — привязки по осям; точки ближе 120 мм одна к другой в цепочку не дробятся — их привязки только в таблице.
3. У знака — марка электроточки (Р — розетка, S — выключатель, Св — светильник, ЭВ — вывод кабеля); условные обозначения и общие указания — лист 3.

					Проект: Квартира 58 м²	М 1:20
	Лист	№ док.	Подпись	Дата		
Дизайнер	Кырлан А.С.			04.11.26	Привязки электроточек, стена В. Прихожая (пом. 5)	Стадия: П; Лист: 59; Листов: 71

Развёртка стены А

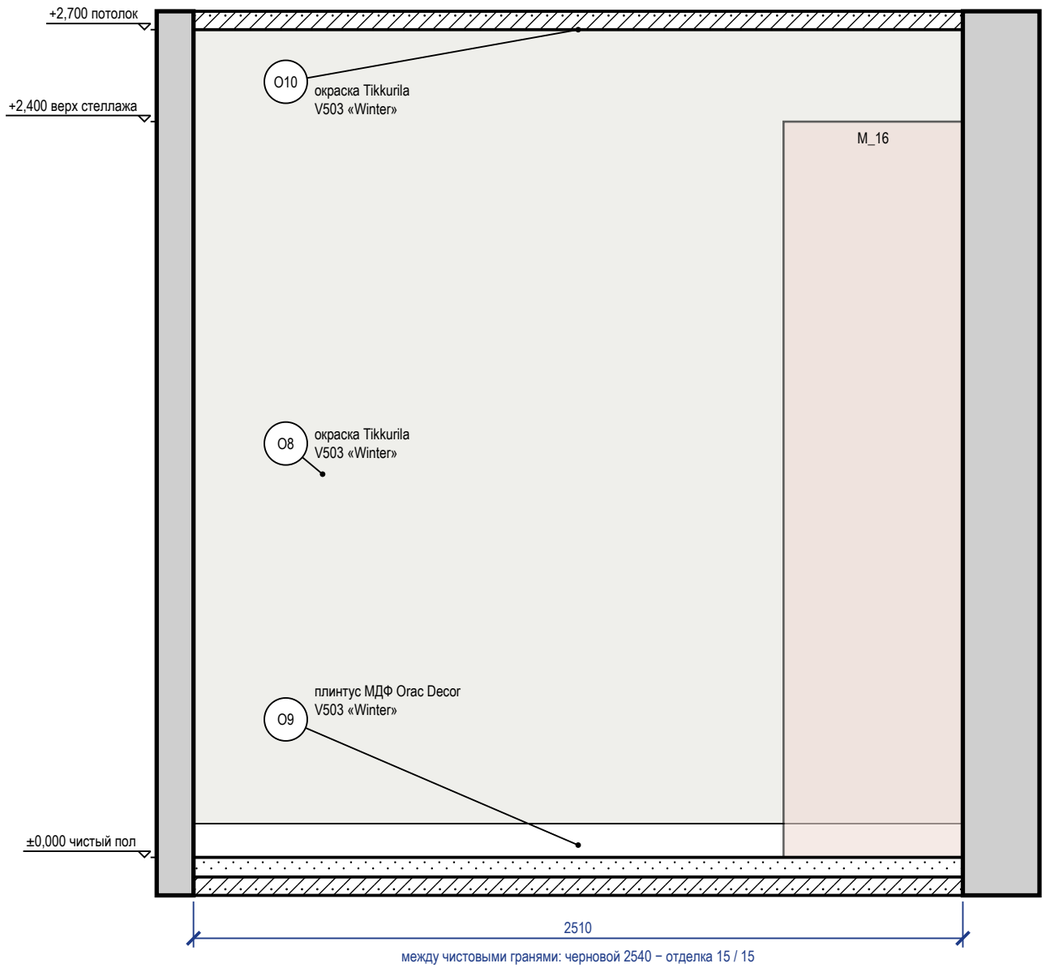

Развёртка стены Б


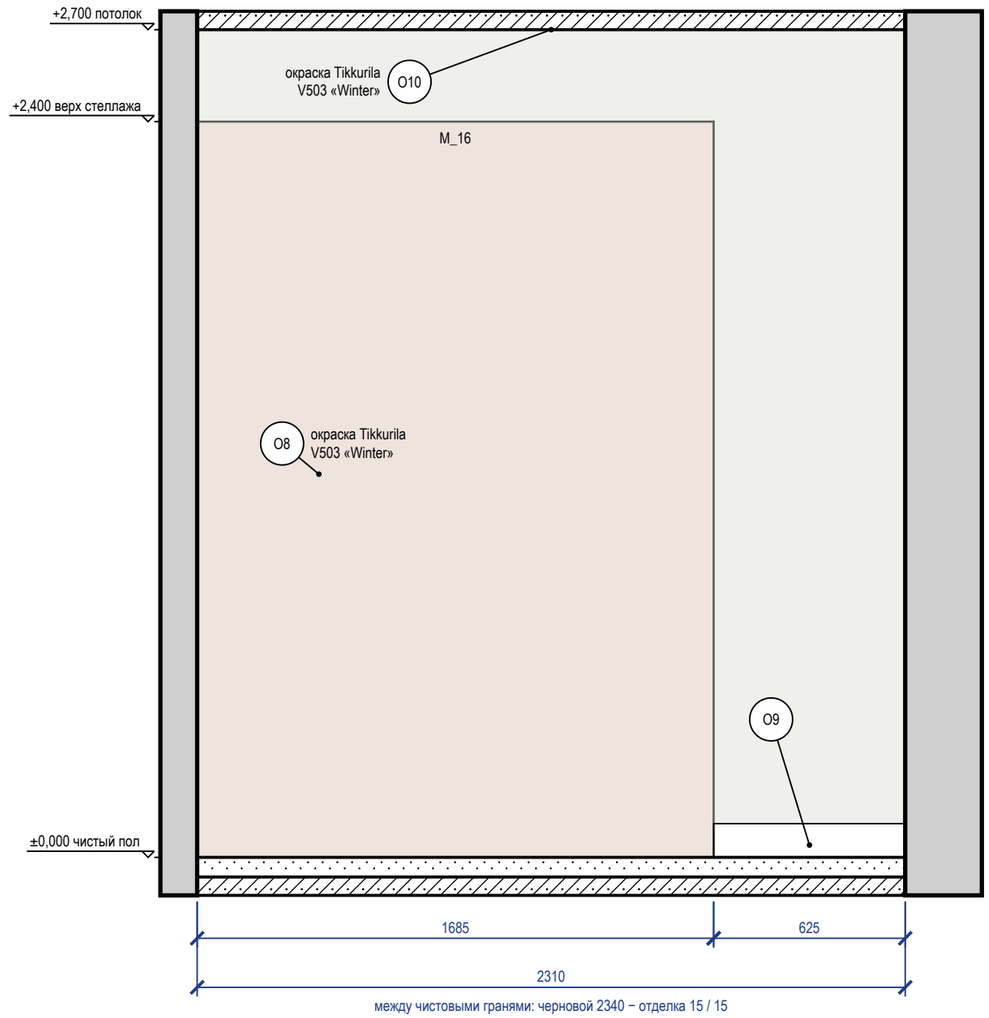


Схема развёрток (М 1:100)

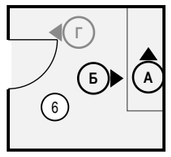

Ведомость отделки (на листе)

Марка	Поверхность	Материал, изделие	Цвет, код	Кол.
O8	стены	окраска, Tikkurila Harmony, матовая, подготовка Q3	Tikkurila V503 «Winter»	13 м²
O9	плинтус	плинтус МДФ, Orac Decor Luxxus, h 110 мм, SX184	Tikkurila V503 «Winter»	3,1 м
O10	потолок	окраска, Tikkurila Anti-Reflex 2, глубокоматовая, подготовка Q3	Tikkurila V503 «Winter»	5,9 м²

Примечания

1. Размеры — в мм от чистовых поверхностей стен; условные обозначения и общие указания — лист 3.

					Проект: Квартира 58 м²	М 1:20
	Лист	№ док.	Подпись	Дата		
Дизайнер	Кырлан А.С.			04.11.26	Развёртки стен А, Б. Гардеробная (пом. 6)	
					Стадия: П	Лист: 60 / Листов: 71

Развёртка стены Г


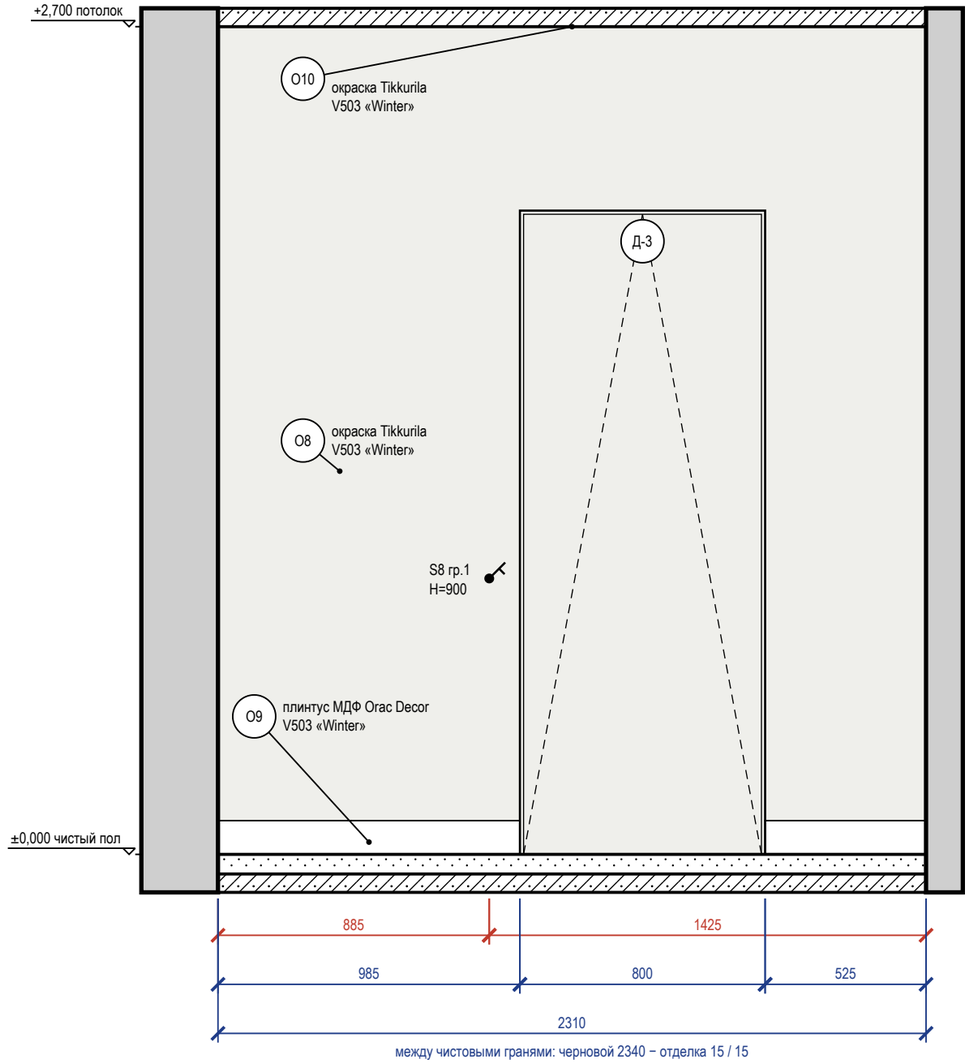


Схема развёрток (М 1:100)

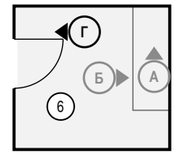

Ведомость отделки (на листе)

Марка	Поверхность	Материал, изделие	Цвет, код	Кол.
О8	стены	окраска, Tikkurila Harmony, матовая, подготовка Q3	Tikkurila V503 «Winter»	4,6 м²
О9	плинтус	плинтус МДФ, Orac Decor Luxxus, h 110 мм, SX184	Tikkurila V503 «Winter»	1,5 м
О10	потолок	окраска, Tikkurila Anti-Reflex 2, глубокоматовая, подготовка Q3	Tikkurila V503 «Winter»	5,9 м²

Примечания

1. Размеры — в мм от чистовых поверхностей стен; условные обозначения и общие указания — лист 3.
2. Двери скрытого монтажа — полотно в плоскости стены, отделка стены по полотну, плинтус прерывается у короба (узел — на листе узлов).

					Проект: Квартира 58 м²	М 1:20
	Лист	№ док.	Подпись	Дата		
Дизайнер	Кырлан А.С.			04.11.26	Развёртка стены Г. Гардеробная (пом. 6)	Стадия: П; Лист: 61; Листов: 71

Комплект предварительный по пунктам этих таблиц. Пока по пункту нет ответа или решения, показанное на указанном листе — допущение проектировщика, а не утверждённое решение.
Сводка: открытых вопросов — 7 (из них ждут факта объекта — 6: контрольного обмера, обследования или документа); изменений в реестре — 3, из них без подписи — 3.

Открытые вопросы и принятые допущения

№	Формулировка	Вид	Кто решает	Если решения нет	Лист, где это проявляется
К-1	Вентканалы на плане заказчика не показаны: ВК-1 принят у перегородки ванной и санузла (со стороны прихожей), ВК-2 — у кухни. От них зависят решётки ВР1–ВР3 и короба. Замерить положение и сечение каналов, проверить тягу.	Отсутствует Ждёт: обмера	Инженер ОВ	решётки ванной и санузла — у ВК-1, кухни — у ВК-2; места — до обмера, лист перевыпустить по факту	л. 37 — План вентиляции
К-2	Ванная (пом. 3), 2140 × 1380 мм в чистоте, проём Д-4 у стены Б. Расстановка проектировщика: ванна 1500 × 700 у стены А от стены Г (была 1600 и заходила в проход перед Д-4 — свободно 240 из 700 мм), умывальник С_03 у стены В справа от ванны — перед ним свободно 750 мм (был напротив ванны в 230 мм), полотенцесушитель С_04 на стене В между коробом стояков и умывальником. Унитаз П2 из образца раскладки снят: он стоял на стояке Ст К1-1 (короба и люка не поставить), унитаз квартиры — С_05 в санузле, инсталляция и короб — там. Остаётся: перед ванной 680 мм до стены В при ориентире 750 мм — это глубина помещения; у умывальника до стены Б 90 мм при ориентире 200 мм. Решить: (а) принять расстановку; (б) душ с поддоном 900 × 900 у стены Г вместо ванны — перед приборами ≥ 750 мм, кадры ванной перерисовать; (в) другой вариант автора.	Спорно Ждёт: решения	Инженер ВК (вода, канализация)	ванна 1500 × 700 и умывальник у стены В по листам; модели ванны и умывальника не заказывать до решения	л. 14 — План выводов сантехники л. 11 — План размещения мебели и оборудования
К-3	Скрытые двери Д-2, Д-3, Д-4 стоят в существующих проёмах прихожей, размеров в свету нет: короб скрытой двери шире и выше полотна на 100–120 / 50–80 мм, полотно по проёму 2100 под ряд 2000 не встаёт (по каталогам нужно 2050–2080). У Д-3 (спальня) и Д-4 (санузел) откос от угла 40 мм — под короб нужно не меньше 50. Замерить проёмы в чистоте и откосы; решить: проёмы подрезать/расширить на 10+ мм от угла (если стена не несущая) или взять модель с узким коробом; высоту проёма — по выбранной модели.	Отсутствует Ждёт: обмера, затем решения	Архитектор-планировщик	блоки скрытых дверей не заказывать до замера; полотна на листах — расчётные («расч.»), проёмы не переносятся	л. 26 — План размещения дверей
К-4	Климатический подрайон (СП 131.13330) не задан: принят не северный — жилые комнаты и кухня под потолком от 2,5 м (СП 54, п. 5.12); в IA, IБ, IГ, IД, IVA — от 2,7 м.	Отсутствует Ждёт: документа	Архитектор-планировщик	отметки потолков жилых — по 2,5 м; при северном подрайоне уровни ниже 2,7 м пересчитать до заказа каркаса	л. 28 — План потолков
К-5	Основа альбома — план заказчика без контрольного обмера: размеры помещений сняты с плана, высота потолка 2700 мм и толщины стен (наружные 250 мм, перегородки 120 мм) приняты — на плане они не указаны. От них зависят вертикальные размеры (развёртки, шкафы, плитка, потолки), объёмы работ и сборка шкафов-купе. Выполнить контрольный обмер.	Непонятно Ждёт: обмера	Архитектор-планировщик	размеры, высота потолка и толщины стен — принятые; мебель на заказ, двери и каркас потолков не заказывать до обмера	л. 5 — План планировки от заказчика
К-6	Разрешённая мощность 15 кВт принята по типовой квартире, технических условий в материалах объекта нет. Сверить с техническими условиями.	Непонятно Ждёт: документа	Инженер-электрик	вводной аппарат и группы щита — по 15 кВт; при меньшей мощности схему щита пересчитать до монтажа	л. 31 — Однолинейная схема щита
К-7	Места стиральной машины в квартире не было. В ванной 2,2 × 1,5 м и санузле места 600 × 600 с подходом нет. Предложение исполнителя: узкая машина 600 × 450 под столешницей кухни вместо модуля с ящиками М_05 справа от варочной, ряд удлиняется на 220 мм; отдельная группа щита с УЗО 30 мА. Решить: принять, или машина в ванной вместо ванны (душ), или отказ от машины (прачечная) решением автора	Предложение Ждёт: документа, затем решения	Инженер ВК (вода, канализация)	стиральная машина ОБ_02 в кухне под столешницей (ниша вместо М_05, 2800…3420) — как на листах	л. 14 — План выводов сантехники л. 11 — План размещения мебели и оборудования л. 31 — Однолинейная схема щита

Изменения проекта после выпуска листов (реестр изменений)

№	Дата	Лист	Было	Стало	Кто решил, подпись
ИЗ-1	30.10.2026	л. 32 — План розеток и электровыводов л. 36 — Управление светильниками л. 34 — План освещения л. 13 — Ведомости изделий, техники и фурнитуры	Кухня-гостиная: ТВ1, LAN1 и розетка «ТВ, приставка» стояли на стене В (привязка 3300…3450, кухонная стена), а ТВ-тумба ОБ_01 — на стене Г (1500…3300): за телевизором точек не было. Выключатель S1 — на стене Г в зоне экрана, у двери Д-2 выключателя не было. Светильник гардеробной Св16 — на линии L6 подсветки кухонной столешницы, выключателя в гардеробной нет. Ванная и санузел — одна линия L4 с одним выключателем S4. Вытяжка в М_07 без вывода питания; розетка холодильника без привязки к модулю М_01.	ТВ1 (2400), LAN1 (2550) и розетка приставки (2400, H=300) — на стене Г по оси тумбы ОБ_01. S1 — стена В, привязка 4950 (150 мм от проёма Д-2 со стороны ручки), S5 у дивана — проходной. Св16 — линия L7, выключатель S8 на стене Г гардеробной у Д-3 (привязка 1500). Санузел — линия L9, выключатель S9 в прихожей у Д-4 санузла (стена Г, привязка 1450); S4 — только ванная (L4, вентилятор ВР2). Розетка вытяжки — стена В привязка 2500, H=2200, группа 2 (для М_07); розетка холодильника — для М_01.	Не утверждено: подписи нет. решение исполнителя; на утверждение А. С. Кырлана

					Проект: Квартира 58 м²
	Лист	№ док.	Подпись	Дата	Открытые вопросы, принятые допущения и конфликты. Лист 1 из 2
Дизайнер	Кырлан А.С.			04.11.26	

Стадия	Лист	Листов
П	62	71

Изменения проекта после выпуска листов (реестр изменений) (продолжение)


№	Дата	Лист	Было	Стало	Кто решил, подпись
ИЗ-2	30.10.2026	л. 11 — План размещения мебели и оборудования л. 12 — Спецификация мебели и оборудования	Диван М_08 на стене Б привязка 1300…3500: торец в 500 мм от стены В, дверь Д-2 (3900…4800) открывалась в торец дивана. Кресло М_11 х 4250, у 450.	Диван М_08 привязка 1000…3200 — перед проёмом 800 мм; кресло М_11 х 3500…4300, у 450 у окна 2. Выключатель S5 и розетка у дивана — привязка 900. Знак «**» у М_08, М_11 до подписи автора.	Не утверждено: подписи нет. решение исполнителя; предложение проектировщика, на утверждение А. С. Кырлана
ИЗ-3	30.10.2026	л. 37 — План вентиляции	Внутренний блок КВ-1 на стене А привязка 3300…4200 — внутри оконного проёма 3200…4800; наружный КН-1 привязка 3350 — на окне.	КВ-1 — стена Г, привязка 300…1200 (простенок у окна 1), КН-1 — стена А, простенок между окнами 2400…3200. Трасса ≈ 3 м (петля принята по минимуму, паспорта модели нет). Знак «**» у КВ-1 до подписи автора.	Не утверждено: подписи нет. решение исполнителя; предложение проектировщика, на утверждение А. С. Кырлана

Примечания


1. Номера листов — по ведомости рабочих чертежей комплекта (лист «Общие данные»).
2. Графа «Если решения нет» показывает состояние решения на листах; влияние на сроки и стоимость по пунктам не оценивалось.
3. Пункт, по которому принято решение, при следующем выпуске комплекта из таблиц исключается.

					Проект: Квартира 58 м²		
	Лист	№ док.	Подпись	Дата	Открытые вопросы, принятые допущения и конфликты. Лист 2 из 2	Стадия	Лист	Листов
Дизайнер	Кырлан А.С.			04.11.26		П	63	71


Вид с фасадами

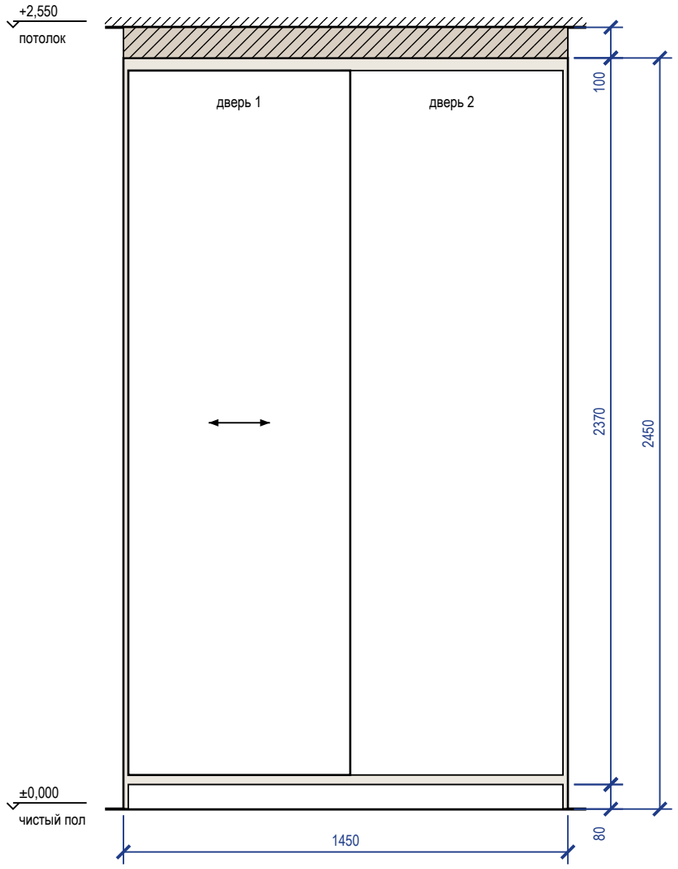


Вид без фасадов

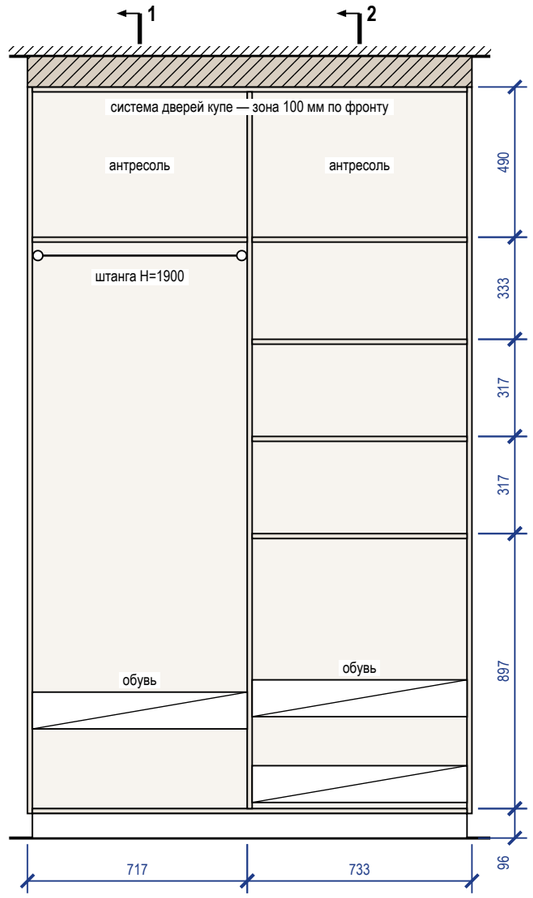

Разрез 1-1

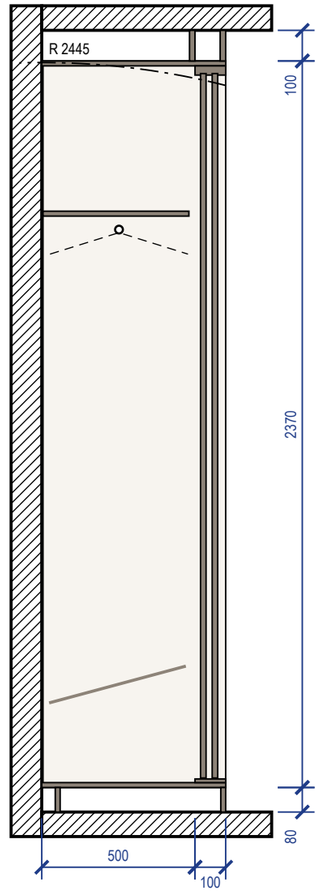


Разрез 2-2

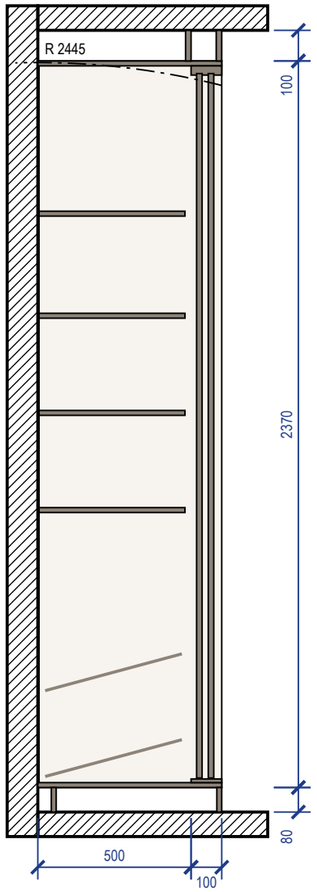

Примечания


1. Размеры — в мм по чистовой отделке; изделие 1450×600×2450 (Ш×Г×В). Перед раскроем — контрольный замер цеха после чистовой отделки стен, пола и потолка.
2. Корпус — ЛДСП 16 мм, задняя стенка ХДФ 4 мм в паз, цоколь 80 мм на регулируемых опорах; двери купе — ЛДСП 10 мм в алюминиевом профиле; нахлёст 30 мм, ширина двери 724 мм, высота — проём минус 40 мм; цвет — по колерной карте.
3. Кромка: скрытые торцы 0,4 мм, видимые 1 мм (ПВХ/АБС).
4. Номинальные зазоры: дверь купе — боковина 3 мм, фасад ящика — стойка 2 мм; ящики внутри купе — с накладкой 30 мм на стойке со стороны нахлёста дверей.
5. Присадка по 32-й системе — выполняет цех.
6. Компенсатор 100 мм — короб из ЛДСП по фронту и торцам, подгоняется к потолку при монтаже (припуск 20 мм), крепится к корпусу и к потолку.
7. Подъём корпуса: диагональ боковины без цоколя $\sqrt{(2370^2 + 600^2)} = 2445$ мм < 2550 мм до потолка — корпус собирается лёжа, поднимается поворотом и ставится на цоколь.
8. Крепление к стене от опрокидывания — уголки 2 шт. к несущему основанию (монтажная схема шкафов).

3D орто

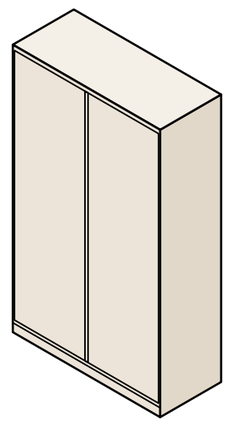


					Проект: Квартира 58 м²	М 1:20
	Лист	№ док.	Подпись	Дата		
Дизайнер	Кырлан А.С.			04.11.26	Шкаф-купе М_15	Стадия: П; Лист: Д_1; Листов: 71


Общий вид

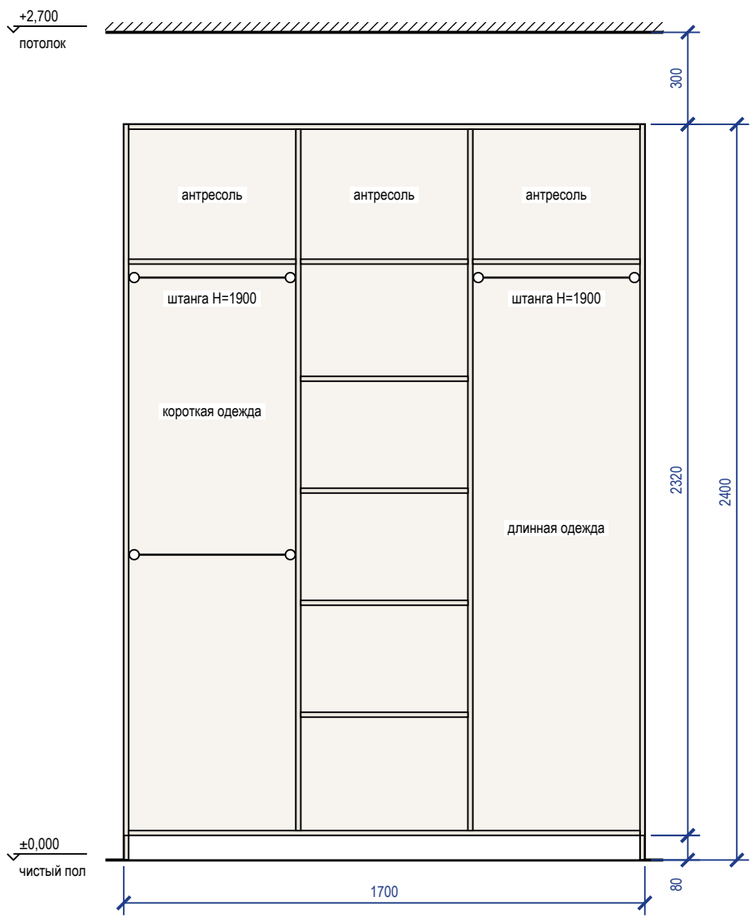


Наполнение, размеры в свету

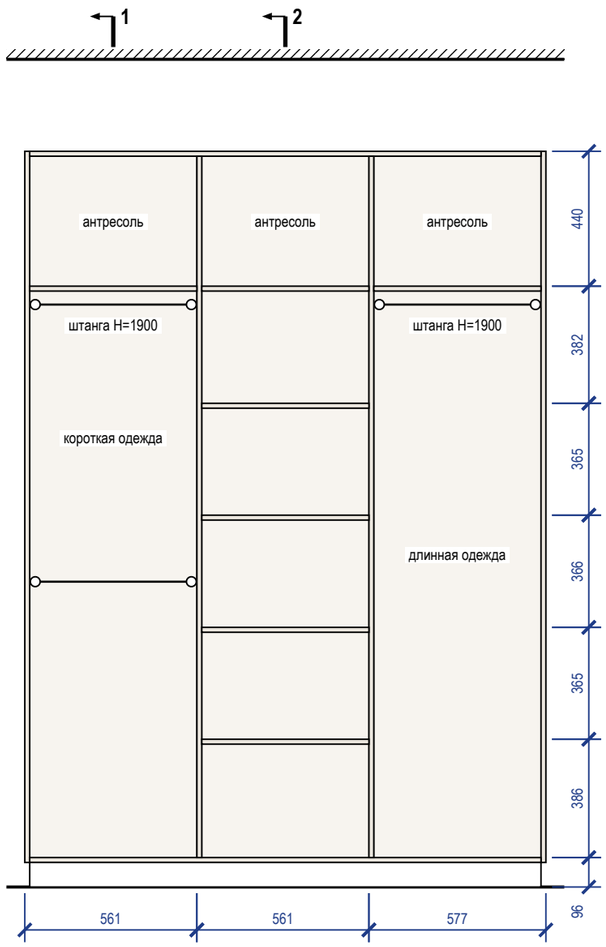

Разрез 1-1

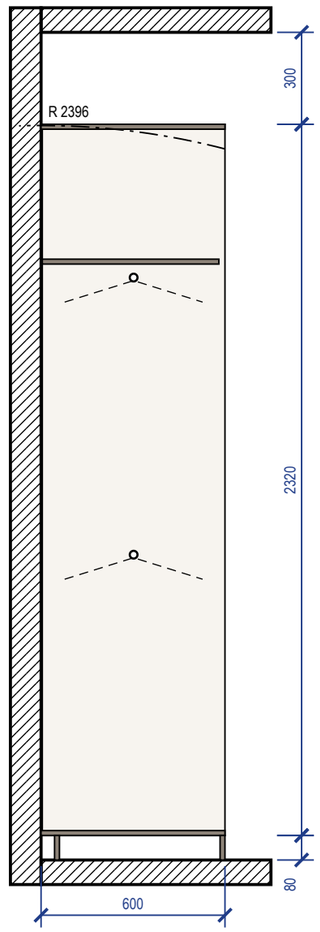


Разрез 2-2

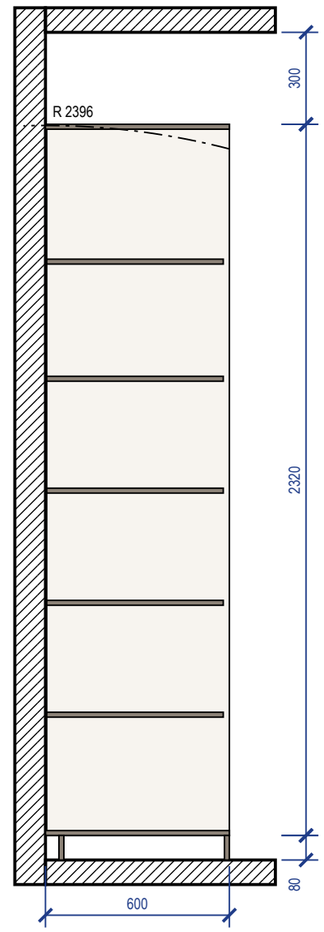

Примечания


1. Размеры — в мм по чистовой отделке; изделие 1700×600×2400 (Ш×Г×В). Перед раскроем — контрольный замер цеха после чистовой отделки стен, пола и потолка.
2. Корпус — ЛДСП 16 мм, задняя стенка ХДФ 4 мм в паз, цоколь 80 мм на регулируемых опорах; открытая система: без фасадов.
3. Кромка: скрытые торцы 0,4 мм, видимые 2 мм (ПВХ/АБС).
4. Присадка по 32-й системе — выполняет цех.
5. Зазор до потолка 300 мм.
6. Подъём корпуса: диагональ боковины без цоколя √(2320² + 600²) = 2396 мм < 2700 мм до потолка — корпус собирается лёжа, поднимается поворотом и ставится на цоколь.
7. Крепление к стене от опрокидывания: крепление к стене, 3 точки; основание стены и шаг анкеров — монтажная схема шкафов.

3D орто

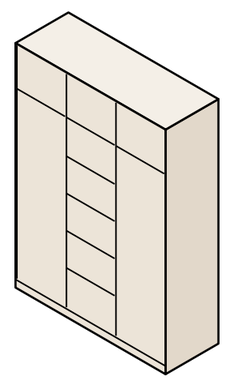


					Проект: Квартира 58 м²	**М 1:20**
	Лист	№ док.	Подпись	Дата	Система хранения М_16	Стадия / Лист / Листов
Дизайнер	Кырлан А.С.			04.11.26		П / Д_2 / 71


Вид с фасадами

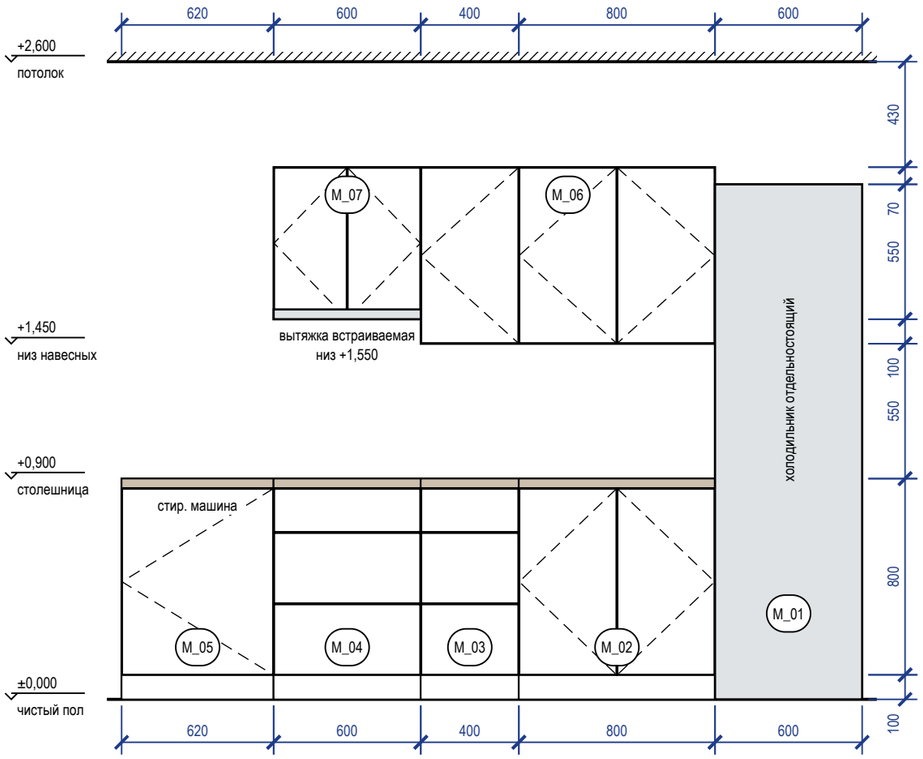


Вид без фасадов (наполнение, выводы)

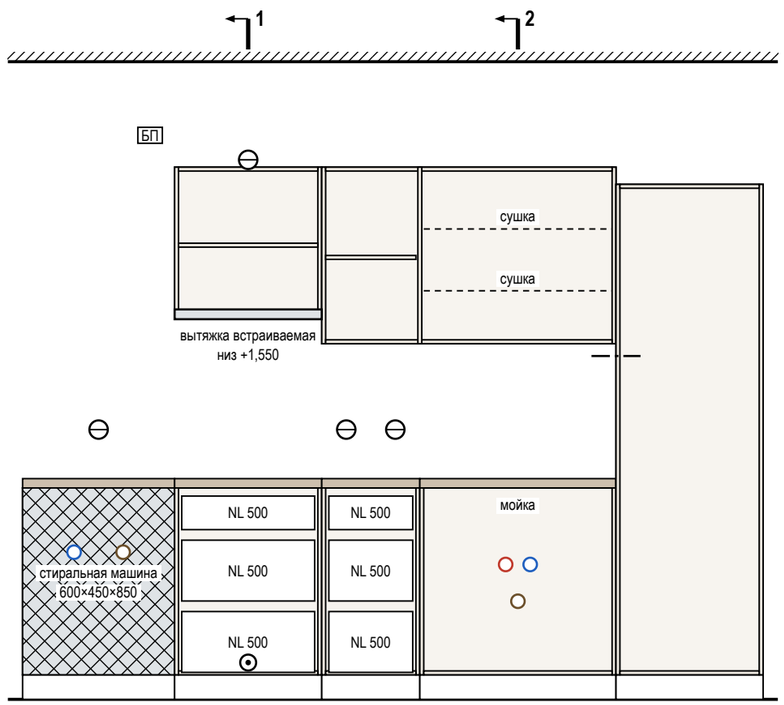


Разрез 1-1

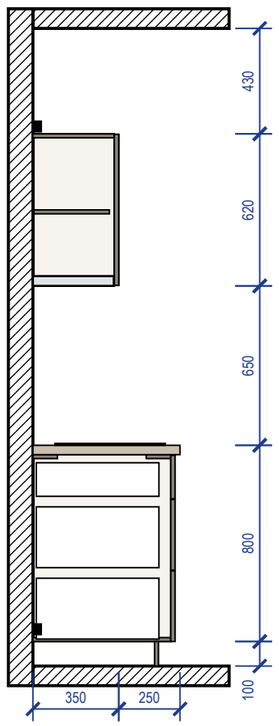

Разрез 2-2

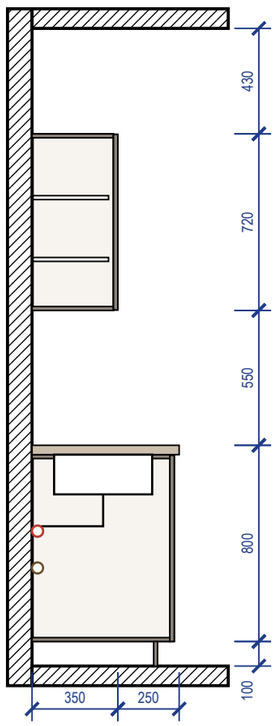

3D орто

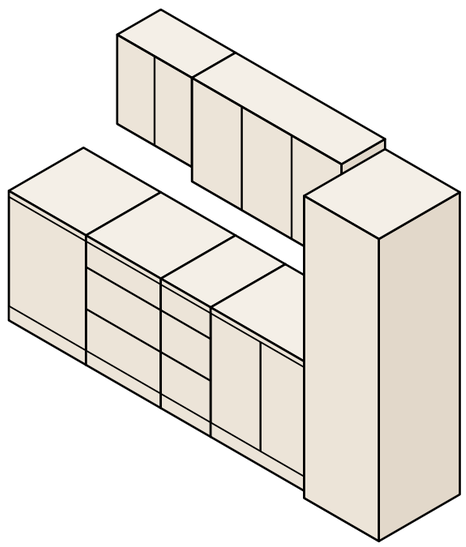

Примечания

1. Размеры — в мм по чистовой отделке, вид из помещения; марки — как на плане расстановки. Перед раскроем — контрольный замер цеха после фартука и пола.
2. Корпуса — ЛДСП 16 мм, задняя стенка ХДФ 4 мм; фасады — МДФ эмаль 18 мм, цвет по колерной карте; столешница 38 мм, свес 20 мм; цоколь 100 мм.
3. Кромка: скрытые торцы 0,4 мм, видимые 1 мм. Номинальные зазоры: между фасадами 3 мм, фасад — столешница 3 мм, фасад — стена не менее 3 мм.
4. Ящики полного выдвижения и петли — с доводчиком; присадка по 32-й системе — выполняет цех.
5. Вытяжка встраивается в дно навесного модуля M_07 над варочной: её низ на 1550 мм от пола, 650 мм над панелью (не меньше 650 мм).
6. Ниши техники — по монтажным схемам выбранных моделей: решётка в цоколе и канал за пеналом холодильника, зазор за духовым шкафом, фасад ПММ на двери машины.

					Проект: Квартира 58 м²	**М 1:25**
	Лист	№ док.	Подпись	Дата		
Дизайнер	Кырлан А.С.			04.11.26	Кухня (пом. 1). Развёртка гарнитура	
					Стадия: П	Лист: Д_3 / Листов: 71

выпуск 04.11.2026 № e0dc2f2b59 · стр. 66 из 71

Ведомость отделки помещений (форма 1 прил. А ГОСТ 21.501-2018)

№	Наименование помещения	Потолок			Стены и перегородки			Низ стен (плинтус)			Пол		Примечание
		Вид отделки	Код цвета	S, м²	Вид отделки	Код цвета	S, м²	Вид отделки	Код цвета	L, м	Вид отделки	S, м²	
1	Кухня-гостиная 21,04 м²	ГКЛ по каркасу П113, отм. +2,600; +2,550; окраска, Tikkurila, глубокоматовая	NCS S 0300-N	21,04	Окраска, Tikkurila, полуматовая, подготовка Q3	NCS S 1002-Y50R	41,25	Плинтус МДФ h=110 мм, SX184	NCS S 0300-N	17,7	Аналог: инженерная доска, дуб натуральный, масло, 1-полосная, 14/4 мм, на клею; тип 1, отм. ЧП ±0,000	21,04	Н стен 2600 (до потолка)
2	Спальня 13,95 м²	ГКЛ по каркасу П113, отм. +2,600; +2,550; окраска, Tikkurila, глубокоматовая	NCS S 0300-N	13,95	Окраска, Tikkurila, глубокоматовая, подготовка Q3	NCS S 1502-Y50R	33,91	Плинтус МДФ h=110 мм, SX184	NCS S 0300-N	14,2	Аналог: инженерная доска, дуб натуральный, масло, 1-полосная, 14/4 мм, на клею; тип 1, отм. ЧП ±0,000	13,95	Н стен 2550 (до потолка)
3	Ванная 2,95 м²	ГКЛВ по каркасу П113, отм. +2,600; окраска, Tikkurila, глубокоматовая	NCS S 0300-N	2,95	Облицовка плиткой, 610015000370, 600×1200 мм, клей С2	Italon 610015000370	16,94	нет (облицовка от пола)			Керамогранит, SG651622R, 600×600 мм; тип 2, отм. ЧП −0,015	2,95	Н стен 2615 (до потолка); тёплый пол; гидроизоляция обмазочная, 2 слоя, с заведением на стены 200 мм; над ванной — до 2000 и 300 мм за борт (по пирогу пола); тест проливом и акт скрытых работ
4	Санузел 1,80 м²	ГКЛВ по каркасу П113, отм. +2,600; окраска, Tikkurila, глубокоматовая	NCS S 0300-N	1,80	Облицовка плиткой, 610015000370, 600×1200 мм, клей С2	Italon 610015000370	14,12	нет (облицовка от пола)			Керамогранит, SG651622R, 600×600 мм; тип 2, отм. ЧП −0,015	1,80	Н стен 2615 (до потолка); гидроизоляция обмазочная, 2 слоя, с заведением на стены 200 мм (по пирогу пола); тест проливом и акт скрытых работ
5	Прихожая 9,55 м²	ГКЛ по каркасу П113, отм. +2,550; +2,600; окраска, Tikkurila, глубокоматовая	NCS S 0300-N	9,55	Окраска, Tikkurila, полуматовая, подготовка Q3	NCS S 1502-Y50R	22,66	Плинтус МДФ h=110 мм, SX184	NCS S 0300-N	8,0	Керамогранит, SG651622R, 600×600 мм; тип 3, отм. ЧП ±0,000	9,55	Н стен 2550 (до потолка)
6	Гардеробная 5,94 м²	Существующий потолок, отм. +2,700; окраска, Tikkurila Anti-Reflex 2, глубокоматовая, 2 слоя, подготовка Q3	Tikkurila V503	5,94	Окраска, Tikkurila Harmony, матовая, 2 слоя, подготовка Q3	Tikkurila V503	24,67	Плинтус МДФ h=110 мм, SX184	Tikkurila V503	9,0	Аналог: инженерная доска, дуб натуральный, масло, 1-полосная, 14/4 мм, на клею; тип 1, отм. ЧП ±0,000	5,94	Н стен 2700 (до потолка); плинтус в цвет: стены
	Итого			**55,23**			**153,54**			**48,8**		**55,23**	

Сводка площадей по материалам отделки

Поверхность	Материал / код цвета	Серия	Площадь, м²
Потолок	NCS S 0300-N		49,29
Потолок	Tikkurila V503	Anti-Reflex 2	5,94
Стены	NCS S 1002-Y50R		41,25
Стены	NCS S 1502-Y50R		56,57
Стены	облицовка плиткой 600×1200 мм, Italon 610015000370	610015000370	31,05
Стены	Tikkurila V503	Harmony	24,67

Примечания

1. Площади поверхностей — по чистым граням стен до отделки: стены = периметр × высоту от чистого пола помещения до низа потолка минус проёмы (облицовка плиткой — до верха облицовки); плинтус = периметр минус дверные проёмы; пол и потолок — по площади помещения. Количество плиток по раскладке. Площади помещений — с учётом всех частей помещения; откосы в площадь стен не входят.
2. Акцентные стены — отдельными строками, их площадь вычтена из основной отделки стен помещения.
3. Плинтус — длина по периметру за вычетом дверных проёмов; примыкания к наличникам и встроенной мебели — по развёрткам.
4. Формат плитки — Ш×В×Т (ширина × высота в положении укладки × толщина), мм; на полу — вдоль стен А/В × вдоль стен Б/Г.
5. Коды цвета — по веерам производителей; колеровка каждой краски одной партией, проверка выкраса при свете D65 и при лампах проекта.
6. Уровни подготовки Q1–Q4 — система Knauf, не норма ГОСТ/СП; допуски поверхностей — по СП 71.13330.2017 (действующая редакция).
7. «аналог:» — изделие задано характеристиками, марку и артикул согласовать с заказчиком до закупки.

					Проект: Квартира 58 м²
	Лист	№ док.	Подпись	Дата	Ведомость отделки помещений
Дизайнер	Кырлан А.С.			04.11.26	

Стадия	Лист	Листов
П	С1	71

Поз.	Наименование и техническая характеристика	Тип, марка, обозначение документа	Код продукции	Поставщик	Ед. изм.	Кол.	Образец	Примечание
	Лакокрасочные материалы							
1	Краска интерьерная водно-дисперсионная акриловая для стен, полуматовая, класс мокрого истирания 1 по EN 13300, база A; цвет NCS S 1002-Y50R, колеровка машинная	Tikkurila		Tikkurila	л	11,7		поз. К1 колерной карты; пом. 1; S = 41,2 м² × 2 сл. × 0,12 л/м² = 9,9 л, +10 % и 0,5 л на подкраску → ≥ 11,4 л; тара 1 × 9 л + 1 × 2,7 л
2	Краска интерьерная водно-дисперсионная для потолков, глубокоматовая, класс мокрого истирания 1 по EN 13300, база A; цвет NCS S 0300-N, колеровка машинная	Tikkurila		Tikkurila	л	9,9		поз. К2 колерной карты; пом. 1, 3, 4, 5; S = 35,3 м² × 2 сл. × 0,12 л/м² = 8,5 л, +10 % и 0,5 л на подкраску → ≥ 9,8 л; тара 1 × 9 л + 1 × 0,9 л
3	Краска интерьерная водно-дисперсионная акриловая для стен, глубокоматовая, класс мокрого истирания 2 по EN 13300, база A; цвет NCS S 1502-Y50R, колеровка машинная	Tikkurila		Tikkurila	л	9,9		поз. К4 колерной карты; пом. 2; S = 33,9 м² × 2 сл. × 0,12 л/м² = 8,1 л, +10 % и 0,5 л на подкраску → ≥ 9,5 л; тара 1 × 9 л + 1 × 0,9 л
4	Краска интерьерная водно-дисперсионная для потолков, глубокоматовая, класс мокрого истирания 2 по EN 13300, база A; цвет NCS S 0300-N, колеровка машинная	Tikkurila		Tikkurila	л	4,5		поз. К5 колерной карты; пом. 2; S = 13,9 м² × 2 сл. × 0,12 л/м² = 3,3 л, +10 % и 0,5 л на подкраску → ≥ 4,2 л; тара 1 × 2,7 л + 2 × 0,9 л
5	Краска интерьерная водно-дисперсионная акриловая для стен, полуматовая, класс мокрого истирания 1 по EN 13300, база A; цвет NCS S 1502-Y50R, колеровка машинная	Tikkurila		Tikkurila	л	7,2		поз. К6 колерной карты; пом. 5; S = 22,7 м² × 2 сл. × 0,12 л/м² = 5,4 л, +10 % и 0,5 л на подкраску → ≥ 6,5 л; тара 2 × 2,7 л + 2 × 0,9 л
6	Краска интерьерная водно-дисперсионная акриловая для стен, матовая, класс мокрого истирания 1 по EN 13300, база A; цвет по вееру Tikkurila V503 «Winter», колеровка машинная	Tikkurila Harmony		Tikkurila	л	7,2		поз. К7 колерной карты; пом. 6; S = 24,7 м² × 2 сл. × 0,12 л/м² = 5,9 л, +10 % и 0,5 л на подкраску → ≥ 7,0 л; тара 2 × 2,7 л + 2 × 0,9 л
7	Краска интерьерная водно-дисперсионная акриловая для потолков, глубокоматовая, класс мокрого истирания 2 по EN 13300, база A; цвет по вееру Tikkurila V503 «Winter», колеровка машинная	Tikkurila Anti-Reflex 2		Tikkurila	л	2,7		поз. К8 колерной карты; пом. 6; S = 5,9 м² × 2 сл. × 0,12 л/м² = 1,4 л, +10 % и 0,5 л на подкраску → ≥ 2,1 л; тара 1 × 2,7 л
8	Акрил, полуматовая в цвет NCS S 0300-N — окраска плинтуса	аналог по характеристикам			л	1,4		поз. К3; пом. 1, 2, 5; L = 39,9 м, S = 5,0 м² × 2 сл. × 0,12 л/м² + 10 %; продукт подобрать в веере NCS
9	Краска для МДФ и дерева в цвет Tikkurila V503 «Winter» — окраска плинтуса; блеск не ниже блеска стен	марка не задана			л	0,5		поз. К9; пом. 6; L = 9,0 м, S = 1,1 м² × 2 сл. × 0,12 л/м² + 10 %; продукт подобрать в веере Tikkurila
10	Грунтовка акриловая под окраску стен и потолков — из системы производителя краски	по системе краски			м²	178		площадь окраски стен, акцентов и потолков; 1 слой перед окраской; расход — по ТУ грунтовки
	Плитка и керамогранит							
11	SG651622R, 600×600 мм, противоскольжение R10	SG651622R		Kerama Marazzi	м²	19,44		шов 2 мм; Ванная, пол; Санузел, пол; Прихожая, пол; по раскладке 48 шт (S = 14,30 м²), с запасом 54 шт
12	610015000370, 1200×600 мм	610015000370		Italon	м²	70,56		шов 2 мм; Ванная, стены А–Г; Ванная, короб стояков Ш1 489×319; Санузел, стены А–Г; Санузел, короб инсталляции; по раскладке 87 шт (S = 31,81 м²), с запасом 98 шт
	Напольные покрытия							
13	Инженерная доска, дуб натуральный, масло, 1-полосная, 14/4 мм, класс 33, эмиссия E1, укладка на клей	аналог по характеристикам			м²	37,5		пом. 1, 2; S = 34,99 м² + 7 % (прямая укладка); к заказу — кратно упаковке
14	Инженерная доска, дуб натуральный, масло, 1-полосная, 14/4 мм, эмиссия E1, укладка на клей	аналог по характеристикам			м²	6,4		пом. 6; S = 5,94 м² + 7 % (прямая укладка); к заказу — кратно упаковке
15	Клей для паркета и инженерной доски, эластичный (СМП / полиуретановый)	по рекомендации производителя доски			м²	41		площадь приклейки; расход и шпатель — по ТУ клея
	Погонажные изделия							
16	SX184, h = 110 мм, крепление к стене, окраска в цвет NCS S 0300-N	SX184		Orac Decor	м	44		пом. 1, 2, 5; L = 39,9 м (периметр без дверных проёмов) + 10 % на подрезку; в штуках — по длине планки
17	SX184, h = 110 мм, крепление к стене, окраска в цвет Tikkurila V503	SX184		Orac Decor	м	10		пом. 6; L = 9,0 м (периметр без дверных проёмов) + 10 % на подрезку; в штуках — по длине планки
	Смеси и материалы для облицовки							
18	Затирка для швов плитки	аналог по характеристикам			кг	3,9		по раскладке (a+b)/(a·b) × шов × t × 1,6 + 10 %
19	Клей плиточный C2 S1 по EN 12004, слой 5 мм	аналог по характеристикам			кг	35		2 меш. по 25 кг; 1,5 кг/м² на 1 мм слоя + 10 %
20	Клей плиточный C2 по EN 12004, слой 5 мм	аналог по характеристикам			кг	332		14 меш. по 25 кг; 1,5 кг/м² на 1 мм слоя + 10 %
21	Гидроизоляция обмазочная мокрых зон: пол, стены по периметру, зоны замачивания; 2 слоя с армирующей лентой в углах	аналог по характеристикам			м²	13,4		площадь по листу раскладки плитки + 10 %; расход смеси — по ТУ
22	Лента демпферная по периметру пола из плитки	аналог по характеристикам			м	21		периметр без дверных проёмов + 10 %

Примечания

1. Количества — из геометрии проекта: площади поверхностей по чистым граням стен до отделки (те же, что в ведомости отделки и колерной карте), плитка, клей и затирка — по раскладке плиточника; в графе «Кол.» — к заказу, с запасом.
2. Краска: расход 0,12 л/м² на слой в 2 слоя, если по ТУ не задан иной; запас 10 % и 0,5 л на подкраску каждого кода. Один код — одна партия, колеровка машинная в колеровочном центре бренда; в заказ — только после утверждения выкраса (колерная карта). Фасовка — по каталогу бренда на дату выпуска; к заказу — не меньше расчётного объёма.
3. «Аналог по характеристикам» — допускается изделие другого производителя с характеристиками не ниже указанных, по согласованию с автором проекта.
4. Графы «Код продукции» и «Масса 1 ед.» не заполнены: коды по классификатору продукции не присвоены, масса единицы до 25 кг (ГОСТ 21.110-2013).
5. Грунтовка и клей для доски указаны площадью обработки; объём — по ТУ выбранного продукта.

					Проект: Квартира 58 м²
	Лист	№ док.	Подпись	Дата	
Дизайнер	Кырлан А.С.			04.11.26	Спецификация отделочных материалов

Стадия	Лист	Листов
П	С2	71

Список покупок: материалы для магазина

№	Что купить	Артикул или характеристика	Нужно с запасом	Брать в магазине	Фасовка	Уточнить в магазине	Помещения	Кто покупает
Покрытия полов и облицовка								
1	Инженерная доска (дуб натуральный, рабочий слой 4 мм, эмиссия E1, прямая укладка)	по характеристике: инженерная доска, дуб натуральный, масло, 1-полосная, 14/4 мм	43,96 м²	44 м²		уточнить в магазине: м² в упаковке	1, 2, 6	по проекту
2	Клей для паркетной и инженерной доски (эластичный, по ТУ изготовителя доски)	на выбор бригады по проекту	41,08 м²			уточнить в магазине: расход и фасовку — по выбранному продукту		бригада
3	Керамогранит 600×600 мм SG651622R	SG651622R	53 шт	54 шт		уточнить в магазине: штук в коробке	3, 4, 5	по проекту
4	Керамогранит 1200×600 мм 610015000370	610015000370	96 шт	98 шт		уточнить в магазине: штук в коробке	3, 4	по проекту
Сухие смеси и гидроизоляция								
5	Клей плиточный цементный класса C2 S1 (ГОСТ Р 56387-2018)	на выбор бригады по проекту	34,29 кг	2 меш.	мешок 25 кг			по проекту
6	Клей плиточный цементный класса C2 (ГОСТ Р 56387-2018)	на выбор бригады по проекту	331,29 кг	14 меш.	мешок 25 кг			по проекту
7	Затирка цементная класса класс не задан, цвет — по колерной карте	на выбор бригады по проекту	3,86 кг	2 упак.	упак. 2 кг			по проекту
8	Гидроизоляция обмазочная полимерная, 2 слоя, лента в углах, манжеты на выводах	на выбор бригады по проекту	7,78 м²			уточнить в магазине: расход и фасовку — по выбранному продукту	3, 4	бригада
9	Лента демпферная по периметру пола из плитки	на выбор бригады по проекту	21,05 м	22 м		уточнить в магазине: фасовку		бригада
10	Смесь цементно-песчаная для стяжки М200 (50 мм, 33 мм)	на выбор бригады по проекту	2,85 м³			уточнить в магазине: расход и фасовку — по выбранному продукту		бригада
11	Смесь штукатурная гипсовая для машинного и ручного нанесения по маякам, слой до 10 мм	на выбор бригады по проекту	27,14 м²			уточнить в магазине: расход и фасовку — по выбранному продукту	6	бригада
Короба из ГКЛВ								
12	Лист ГКЛВ 12,5 мм, 2500 × 1200 мм, обшивка коробов в 2 слоя	на выбор бригады по проекту	4,64 м²	2 лист.	лист 3,00 м²		3	бригада
13	Профиль стальной оцинкованный 27 × 28 мм: каркас коробов (стойки и направляющие)	на выбор бригады по проекту	13,29 м	5 шт	хлыст 3 м			бригада
Слаботочные сети								
14	Кабель домофона — тип по системе поставщика	на выбор бригады по проекту	3,4 м	4 м		уточнить в магазине: длину бухты		бригада
15	Кабель коаксиальный RG-6 (75 Ом) к розеткам ТВ	на выбор бригады по проекту	16,3 м	17 м		уточнить в магазине: длину бухты		бригада
16	Кабель U/UTP кат. 5e (LAN, Wi-Fi и камеры по PoE)	на выбор бригады по проекту	30,1 м	31 м		уточнить в магазине: длину бухты		бригада
17	Гофротруба Ø20 для слаботочных линий, отдельно от силовых	на выбор бригады по проекту	44,8 м	45 м		уточнить в магазине: длину бухты		бригада
18	Розетка компьютерная RJ45, кат. 6, с рамкой и подрозетником	на выбор бригады по проекту	2 шт	2 шт	шт			бригада

					Проект: Квартира 58 м²	
	Лист	№ док.	Подпись	Дата		
Дизайнер	Кырлан А.С.			04.11.26	Список покупок	Стадия: П; Лист: С3; Листов: 71

Список покупок: материалы для магазина (продолжение)

№	Что купить	Артикул или характеристика	Нужно с запасом	Брать в магазине	Фасовка	Уточнить в магазине	Помещения	Кто покупает
19	Розетка телевизионная (коаксиальная) с рамкой и подрозетником	на выбор бригады по проекту	1 шт	1 шт	шт			бригада
20	Трубка или монитор домофона (поставка домофонной организации)	на выбор бригады по проекту	1 шт	1 шт	шт			по проекту
21	Щит слаботочный ЩС: корпус, DIN-рейка, розетки 220 В	на выбор бригады по проекту	1 шт	1 шт	шт			бригада
22	Патч-панель, портов не менее 2	на выбор бригады по проекту	1 шт	1 шт	шт			бригада
Лакокрасочные материалы								
23	Краска интерьерная акриловая, полуматовая, класс истирания 1	Tikkurila S 1002-Y50R	10,89 л	5 банк.	банка 2,7 л		1	по проекту
24	Краска интерьерная водно-дисперсионная, глубокоматовая, класс истирания 1	Tikkurila S 0300-N	13,01 л	5 банк.	банка 2,7 л		1, 2, 3, 4, 5	по проекту
25	Краска интерьерная акриловая, глубокоматовая, класс истирания 2	Tikkurila S 1502-Y50R	8,95 л	4 банк.	банка 2,7 л		2	по проекту
26	Краска интерьерная акриловая, полуматовая, класс истирания 1	Tikkurila S 1502-Y50R	5,98 л	3 банк.	банка 2,7 л		5	по проекту
27	Краска интерьерная акриловая, матовая, класс истирания 1	Tikkurila Harmony V503 «Winter»	6,51 л	3 банк.	банка 2,7 л		6	по проекту
28	Краска интерьерная акриловая, глубокоматовая, класс истирания 2	Tikkurila Anti-Reflex 2 V503 «Winter»	1,57 л	1 банк.	банка 2,7 л		6	по проекту
29	Шпаклёвка финишная полимерная под окраску (стены и потолки, Q3)	на выбор бригады по проекту	195,49 м²			уточнить в магазине: расход и фасовку — по выбранному продукту		бригада
30	Грунтовка акриловая глубокого проникновения, 2 слоя	на выбор бригады по проекту	229,66 м²			уточнить в магазине: расход и фасовку — по выбранному продукту		бригада
Погонажные изделия и потолки								
31	Плинтус напольный МДФ под покраску, h=110 мм, крепление к стене	SX184	53,7 м.п.	23 шт	хлыст 2,4 м		1, 2, 5, 6	по проекту
32	Потолок подвесной ГКЛ/ГКЛВ по каркасу Knauf П113: листы, профили, подвесы, лента, шпаклёвка швов	Knauf П113	49,29 м²			уточнить в магазине: расход и фасовку — по выбранному продукту		по проекту


Примечания

1. «Нужно с запасом» — расход по чертежам и раскладке плюс запас на подрезку и подкраску; «Брать в магазине» — то же количество в единицах, которыми продают (банки, мешки, упаковки, листы, штуки, литры).
2. «Уточнить в магазине» — фасовки этого товара в проекте нет: спросите у продавца, сколько в упаковке, и возьмите целое число упаковок не меньше «Нужно с запасом».
3. Плитку, доску и краску одного цвета берите одной партией (один калибр и тон на помещение) и сохраните чек и номер партии до конца ремонта.
4. «По характеристике» — артикул не выбран: подойдёт любой товар с этими свойствами, согласуйте его с дизайнером до покупки. «Бригада» материал выбирает и закупает бригада по своей технологии.
5. Помещения: 1 — Кухня-гостиная; 2 — Спальня; 3 — Ванная; 4 — Санузел; 5 — Прихожая; 6 — Гардеробная; «—» — материал для нескольких помещений, расход по месту.

					Проект: Квартира 58 м²
	Лист	№ док.	Подпись	Дата	
Дизайнер	Кырлан А.С.			04.11.26	Список покупок (окончание)
					Стадия: П; Лист: С4; Листов: 71


1 Порог 15 мм: мокрая зона — смежное помещение (М 1:5)

Применение: двери Д-4

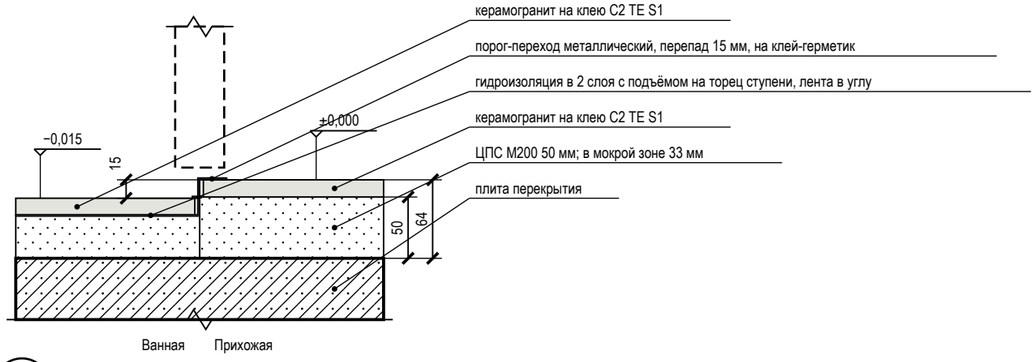


2 Дверь скрытого монтажа в плоскости стены, плинтус (М 1:5)

Применение: двери Д-2, Д-3, Д-4

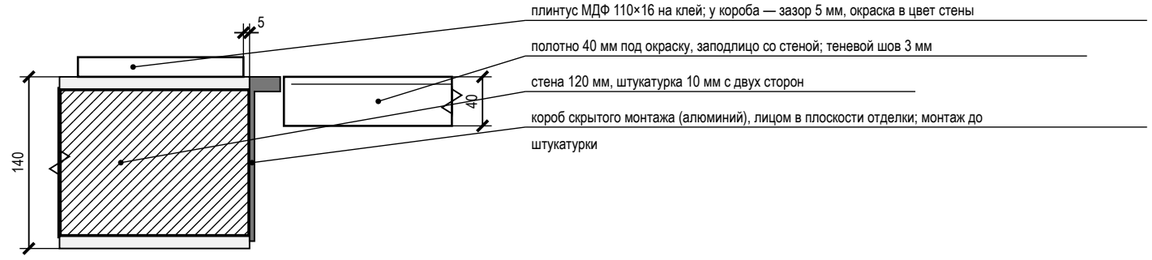


3 Короб стояков К1-1 с люком и звукоизоляцией (М 1:10)

Применение: пом. 3

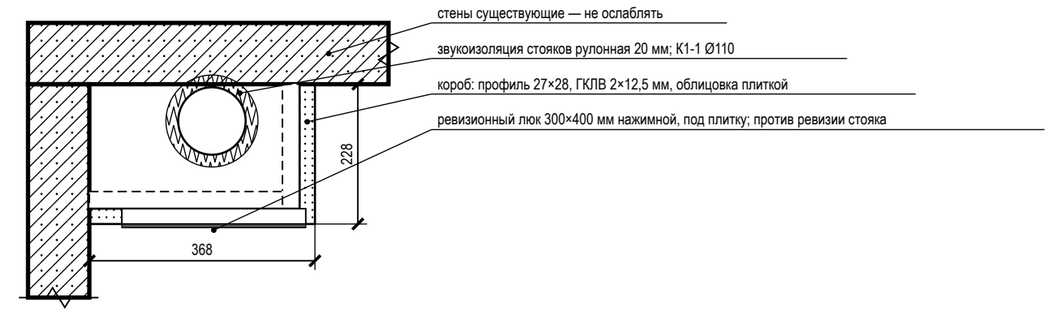


4 Гидроизоляция санузла: заход на стены 200 мм, примыкание ванны (М 1:20)

Применение: пом. 3, 4

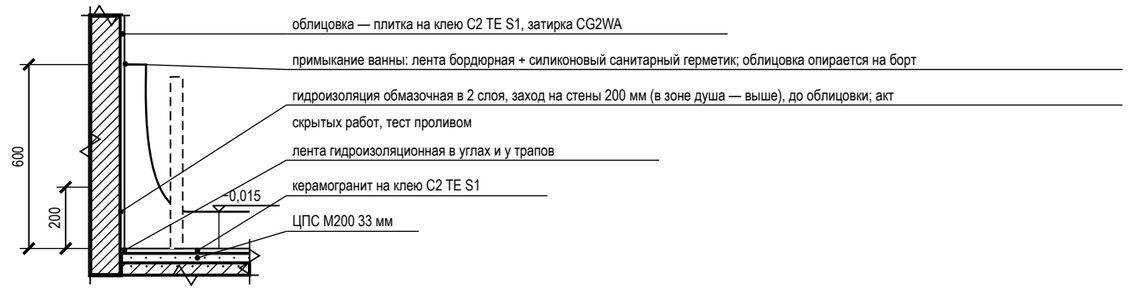


5 Плинтус МДФ 110×16 мм у окрашенной стены по доске (ламинату) (М 1:10)

Применение: пом. 1, 2, 6

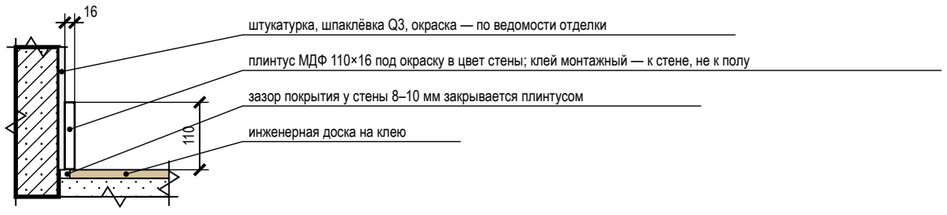

6 Плинтус МДФ 110×16 мм у окрашенной стены по керамограниту (плитке) (М 1:10)

Применение: пом. 5

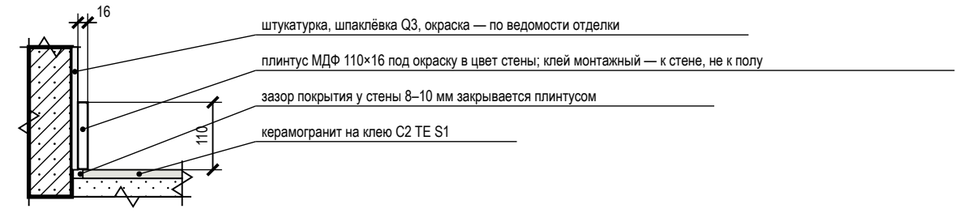

Условные обозначения

- железобетон (плита, стены) — условно: конструкция не установлена
- кладка, перегородка — условно: конструкция не установлена
- стяжка, раствор
- гипсокартон ГКЛВ
- звукоизоляция, эластичный заполнитель
- плитка, керамогранит на клею
- инженерная доска (покрытие пола)
- металлический профиль (порог, Т-профиль, короб двери)
- гидроизоляция (обмазочная, лента)

Примечания

1. Узлы — типовые решения проекта для мест, отмеченных выносками на листе схемы расположения развёрток и узлов; размеры — в мм, отметки — в м от ±0,000.
2. Узлы с гидроизоляцией, закладными и коробами скрытого монтажа принимаются по актам скрытых работ до закрытия отделкой; гидроизоляция — после теста проливом (24 ч).
3. Марки изделий (порог, Т-профиль, короб скрытой двери, люк) — по спецификациям; замена — на аналог с теми же габаритами по согласованию с автором проекта.
4. Материал плиты перекрытия и стен в узлах показан условно (железобетон, кладка): конструкция дома не установлена — крепёж, анкеры и толщины слоёв уточняются после обследования (до него — по допущениям общих указаний).

					Проект: Квартира 58 м²
	Лист	№ док.	Подпись	Дата	Узлы
Дизайнер	Кырлан А.С.			04.11.26	Стадия: П; Лист: С5; Листов: 71

выпуск 04.11.2026 № e0dc2f2b59 · стр. 71 из 71