
ПРЕДВАРИТЕЛЬНО · не для производства работ · открыто пунктов: 8 (реестр — л. 6, 7)

LINEA

ДИЗАЙН-ПРОЕКТ ИНТЕРЬЕРА

# Квартира 101 м²

*ретро с авторской мебелью*

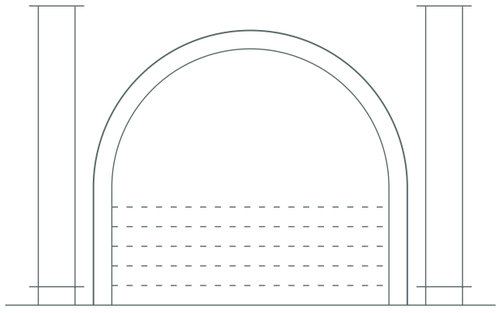

ПАЛИТРА ОТДЕЛКИ

| F&B No. 291 | NCS S 0502-Y | F&B No. 289 | F&B No. 255 | NCS S 1005-Y20 |
|---|---|---|---|---|
| 58 % | 29 % | 10 % | 3 % | текстиль, декор |

АВТОР ПРОЕКТА

Кырлан Александр Сергеевич

Ноябрь 2026



Квартира сверху · схематичная модель по плану

| ОБЩАЯ ПЛОЩАДЬ | ПОМЕЩЕНИЙ | СТАДИЯ | ШИФР | ОСНОВА |
|---|---|---|---|---|
| 100,72 м² | 11, из них жилых 4 | Рабочий проект · предварительно | ГД-2026-009-АИ | план заказчика, без обмера |

| Изм. | Кол.уч | Лист | № док. | Подп. | Дата |
|---|---|---|---|---|---|
| Разраб. | | Кырлан А.С. | | | 04.11.26 |
| Пров. | | | | | |
| ГИП | | | | | |
| | | | | | |
| Н. контр. | | | | | |
| Утв. | | | | | |

**ГД-2026-009-АИ**

Квартира 103 м²

Общая площадь 100,72* м² · * размеры со скана, не замерены (реестр — л. 6, 7, К-1)

| Дизайн-проект интерьера | Стадия | Лист | Листов |
|---|---|---|---|
| | РП | 1 | 120 |

**Титульный лист**

М б/м

Кырлан Александр Сергеевич

выпуск 04.11.2026 № 35b47f1c2a · стр. 1 из 130

# Общие данные

Комплект ГД-2026-009-АИ · Квартира 103 м² · ретро с авторской мебелью

**ПРЕДВАРИТЕЛЬНО · не для производства работ · открыто пунктов: 8 (реестр — л. 6, 7)**

Допущения и предложения на листе. См. лист открытых вопросов (лист 6).

### Ведомость рабочих чертежей основного комплекта ГД-2026-009-АИ

| Лист | Наименование | Примечание |
|---|---|---|
| 1 | Титульный лист | |
| 2 | Общие данные | |
| 3 | Общие данные | |
| 4 | Общие данные | |
| 5 | Общие данные | |
| 6 | Открытые вопросы, принятые допущения и конфликты. Лист 1 из 2 | |
| 7 | Открытые вопросы, принятые допущения и конфликты. Лист 2 из 2 | |
| 8 | Задание на контрольный обмер и обследование. Лист 1 из 3 | |
| 9 | Задание на контрольный обмер и обследование. Лист 2 из 3 | |
| 10 | Задание на контрольный обмер и обследование. Лист 3 из 3 | |
| 11 | График закупок и работ. Лист 1 из 3 | |
| 12 | График закупок и работ. Лист 2 из 3 | |
| 13 | График закупок и работ. Лист 3 из 3 | |
| 14 | Обмерный план | |
| 15 | План демонтажа и монтажа перегородок | |
| 16 | План дверей | |
| 17 | Ведомость заполнения проёмов | |
| 18 | Концепция интерьера | |
| 19 | План расстановки мебели | |
| 20 | Спецификация мебели и оборудования | |
| 21 | Спецификация мебели и оборудования (продолжение) | |
| 22 | Спецификация мебели и оборудования (продолжение) | |
| 23 | План розеток и электровыводов | |
| 24 | План освещения | |
| 25 | План выключателей и схема включения | |
| 26 | Ведомость электроточек и изделий | |
| 27 | Ведомость электроточек и изделий (продолжение) | |
| 28 | Однолинейная схема щита | |
| 29 | План принципиальных трасс | |
| 30 | План слаботочных сетей | |

### Ведомость рабочих чертежей основного комплекта ГД-2026-009-АИ (продолжение)

| Лист | Наименование | Примечание |
|---|---|---|
| 31 | План вентиляции | |
| 32 | План отопления | |
| 33 | План выводов сантехники | |
| 34 | Схема разводки водопровода и канализации | |
| 35 | Аксонометрическая схема В1 (холодное водоснабжение) | |
| 36 | Аксонометрическая схема Т3 (горячее водоснабжение) | |
| 37 | Аксонометрическая схема К1 (канализация) | |
| 38 | Развёртки мокрых зон: выводы ВК. Кухня | |
| 39 | Развёртки мокрых зон: выводы ВК. Ванная | |
| 40 | Развёртки мокрых зон: выводы ВК. Постирочная | |
| 41 | Развёртки мокрых зон: выводы ВК. Ванная мастер | |
| 42 | Спецификация сантехнического оборудования | |
| 43 | Техническое задание на подбор светильников | |
| 44 | Техническое задание на подбор светильников (продолжение) | |
| 45 | План потолков | |
| 46 | Разрезы и узлы потолков | |
| 47 | Разрезы и узлы потолков (продолжение) | |
| 48 | Сечения потолков М 1:10 | |
| 49 | Раскладка плитки. Планы полов | |
| 50 | Раскладка плитки. Прихожая-холл | |
| 51 | Раскладка плитки. Ванная. Развёртки стен | |
| 52 | Раскладка плитки. Ванная мастер. Развёртки стен | |
| 53 | План полов | |

Общие указания — лист 5: ±0,000 — чистый пол; несущие конструкции и сети дома — по отдельному проекту; скрытые работы — по актам. Открытые вопросы и допущения — листы 6, 7.

| Изм. | Кол.уч | Лист | № док. | Подп. | Дата |
|---|---|---|---|---|---|
| Разраб. | | Кырлан А.С. | | | 04.11.26 |
| Пров. | | | | | |
| ГИП | | | | | |
| | | | | | |
| Н. контр. | | | | | |
| Утв. | | | | | |

**ГД-2026-009-АИ**

Квартира 103 м²

Общая площадь 100,72* м² · * размеры со скана, не замерены (реестр — л. 6, 7, К-1)

Дизайн-проект интерьера

| Стадия | Лист | Листов |
|---|---|---|
| РП | 2 | 120 |

**Общие данные**

М б/м

**Кырлан Александр Сергеевич**

выпуск 04.11.2026 № 35b47f1c2a · стр. 2 из 130

# Общие данные

Комплект ГД-2026-009-АИ · лист 2 общих данных (продолжение)

Допущения и предложения на листе. См. лист открытых вопросов (лист 6).

### Ведомость рабочих чертежей основного комплекта ГД-2026-009-АИ (продолжение)

| Лист | Наименование | Примечание |
|---|---|---|
| 54 | Ведомость отделки помещений. Лист 1 из 3 | |
| 55 | Ведомость отделки помещений. Лист 2 из 3 | |
| 56 | Ведомость отделки помещений. Лист 3 из 3 | |
| 57 | Колерная карта | |
| 58 | Колерная карта | |
| 59 | Спецификация отделочных материалов | |
| 60 | Спецификация отделочных материалов | |
| 61 | Концепция декора и визуализации | |
| 62 | План текстиля и декора | |
| 63 | Шторы и карнизы | |
| 64 | Ведомость текстиля | |
| 65 | Ведомость декора. Схемы развески | |
| 66 | Встроенная мебель. Схема расположения | |
| 67 | Система хранения Кл1 | |
| 68 | Шкаф-купе П1 | |
| 69 | Система хранения Пс1 | |
| 70 | Шкаф распашной С2 | |
| 71 | Шкаф распашной М4 | |
| 72 | Кухня (пом. 5). Развёртка гарнитура | |
| 73 | Кухня (пом. 5). Монтажная схема | |
| 74 | Кухня (пом. 5). Развёртка гарнитура | |
| 75 | Кухня (пом. 5). Монтажная схема | |
| 76 | Шкафы. Монтажная схема | |
| 77 | Ведомости изделий, техники и фурнитуры | |
| 78 | Реестр марок отделки и позиций альбома | |
| 79 | Схема расположения развёрток и узлов | |
| 80 | Развёртки стен А, Б. Кабинет-библиотека (пом. 1) | |
| 81 | Развёртки стен В, Г. Кабинет-библиотека (пом. 1) | |
| 82 | Развёртки стен. Кладовая (пом. 2) | |
| 83 | Развёртка стены А. Гостиная-столовая (пом. 3) | |

### Ведомость рабочих чертежей основного комплекта ГД-2026-009-АИ (продолжение)

| Лист | Наименование | Примечание |
|---|---|---|
| 84 | Привязки электроточек, стена А. Гостиная-столовая (пом. 3) | |
| 85 | Развёртка стены Б. Гостиная-столовая (пом. 3) | |
| 86 | Развёртка стены В. Гостиная-столовая (пом. 3) | |
| 87 | Развёртка стены Г. Гостиная-столовая (пом. 3) | |
| 88 | Развёртка стены А. Прихожая-холл (пом. 4) | |
| 89 | Развёртка стены Б. Прихожая-холл (пом. 4) | |
| 90 | Развёртка стены В. Прихожая-холл (пом. 4) | |
| 91 | Развёртка стены Г. Прихожая-холл (пом. 4) | |
| 92 | Развёртки стен Б, В. Кухня (пом. 5), кухонный фронт | |
| 93 | Привязки электроточек и выводов ВК, стена Б. Кухня (пом. 5) | |
| 94 | Развёртки стен А, Г. Кухня (пом. 5) | |
| 95 | Развёртки стен А, Б, В. Ванная (пом. 6) | |
| 96 | Развёртка стены Г. Ванная (пом. 6) | |
| 97 | Привязки электроточек и выводов ВК, стена Г. Ванная (пом. 6) | |
| 98 | Развёртки стен. Постирочная (пом. 7) | |
| 99 | Развёртки стен А, Б. Спальня 2 (пом. 8) | |
| 100 | Развёртка стены В. Спальня 2 (пом. 8) | |
| 101 | Развёртка стены Г. Спальня 2 (пом. 8) | |
| 102 | Развёртка стены А. Коридор (пом. 9) | |
| 103 | Развёртка стены Б. Коридор (пом. 9) | |
| 104 | Развёртка стены В. Коридор (пом. 9) | |
| 105 | Развёртка стены А. Спальня мастер (пом. 10) | |
| 106 | Привязки электроточек, стена А. Спальня мастер (пом. 10) | |

Общие указания — лист 5: ±0,000 — чистый пол; несущие конструкции и сети дома — по отдельному проекту; скрытые работы — по актам. Открытые вопросы и допущения — листы 6, 7.

| Изм. | Кол.уч | Лист | № док. | Подп. | Дата |
|---|---|---|---|---|---|
| Разраб. | | Кырлан А.С. | | | 04.11.26 |
| Пров. | | | | | |
| ГИП | | | | | |
| | | | | | |
| Н. контр. | | | | | |
| Утв. | | | | | |

**ГД-2026-009-АИ**

Квартира 103 м²

Общая площадь 100,72* м² · * размеры со скана, не замерены (реестр — л. 6, 7, К-1)

Дизайн-проект интерьера

| Стадия | Лист | Листов |
|---|---|---|
| РП | 3 | 120 |

**Общие данные**

М б/м

**Кырлан Александр Сергеевич**

выпуск 04.11.2026 № 35b47f1c2a · стр. 3 из 130

# Общие данные

Комплект ГД-2026-009-АИ · лист 3 общих данных (продолжение)

### Ведомость рабочих чертежей основного комплекта ГД-2026-009-АИ (продолжение)

| Лист | Наименование | Примечание |
|---|---|---|
| 107 | Развёртка стены Б. Спальня мастер (пом. 10) | |
| 108 | Развёртки стен В, Г1. Спальня мастер (пом. 10) | |
| 109 | Развёртка стены Г2. Спальня мастер (пом. 10) | |
| 110 | Развёртки стен А, Б, В. Ванная мастер (пом. 11) | |
| 111 | Привязки электроточек и выводов ВК, стена А. Ванная мастер (пом. 11) | |
| 112 | Развёртка стены Г. Ванная мастер (пом. 11) | |
| 113 | Узлы | |
| 114 | Ведомость объёмов работ | |
| 115 | Ведомость объёмов работ (продолжение) | |
| 116 | Ведомость объёмов работ (окончание) | |
| 117 | Спецификация материалов | |
| 118 | Спецификация материалов (окончание) | |
| 119 | Смета ориентировочная | |
| 120 | Смета ориентировочная (окончание) | |

### Ведомость ссылочных и прилагаемых документов

| Обозначение | Наименование | Примечание |
|---|---|---|
| | Ссылочные документы | |
| ГОСТ 21.201-2011 | СПДС. Условные графические изображения элементов зданий, сооружений и конструкций | |
| ГОСТ 21.205-2016 | СПДС. Условные обозначения элементов санитарно-технических систем | |
| ГОСТ 21.210-2014 | СПДС. Изображения условные графические электрооборудования и проводок на планах | |
| ГОСТ 2.306-68 | ЕСКД. Обозначения графические материалов и правила их нанесения на чертежах | |
| | Прилагаемые документы | |
| ГД-2026-009-АИ.В1 | Визуализация. Вид сверху (3D): планировка с мебелью, текстилем и декором | альбом визуализаций |
| ГД-2026-009-АИ.В2 | Визуализация. Интерьер: Ванная (пом. 6), стена Б | |
| ГД-2026-009-АИ.В3 | Визуализация. Интерьер: Ванная (пом. 6), стена В | |
| ГД-2026-009-АИ.В4 | Визуализация. Интерьер: Ванная (пом. 6), стена Г | |
| ГД-2026-009-АИ.В5 | Визуализация. Интерьер: Ванная мастер (пом. 11), общий вид | |

Общие указания — лист 5: ±0,000 — чистый пол; несущие конструкции и сети дома — по отдельному проекту; скрытые работы — по актам. Открытые вопросы и допущения — листы 6, 7.

### Ведомость ссылочных и прилагаемых документов (продолжение)

| Обозначение | Наименование | Примечание |
|---|---|---|
| ГД-2026-009-АИ.В6 | Визуализация. Интерьер: Спальня 2 (пом. 8), стена А | |
| ГД-2026-009-АИ.В7 | Визуализация. Интерьер: Спальня 2 (пом. 8), стена Б | |
| ГД-2026-009-АИ.В8 | Визуализация. Интерьер: Спальня 2 (пом. 8), стена Г | |
| ГД-2026-009-АИ.В9 | Визуализация. Интерьер: Спальня мастер (пом. 10), стена А | |
| ГД-2026-009-АИ.В10 | Визуализация. Интерьер: Спальня мастер (пом. 10), стена Б | |
| ГД-2026-009-АИ.В11 | Визуализация. Интерьер: Спальня мастер (пом. 10), стена В | |
| ГД-2026-009-АИ.В12 | Визуализация. Интерьер: Спальня мастер (пом. 10), стена Г | |
| ГД-2026-009-АИ.В13 | Визуализация. Интерьер: Коридор (пом. 9), стена Б | |
| ГД-2026-009-АИ.В14 | Визуализация. Интерьер: Прихожая-холл (пом. 4), стена А | |
| ГД-2026-009-АИ.В15 | Визуализация. Интерьер: Прихожая-холл (пом. 4), стена Б | |
| ГД-2026-009-АИ.В16 | Визуализация. Интерьер: Кухня (пом. 5), стена Б | |
| ГД-2026-009-АИ.В17 | Визуализация. Интерьер: Кухня (пом. 5), стена В | |
| ГД-2026-009-АИ.В18 | Визуализация. Интерьер: Гостиная-столовая (пом. 3), стена А | |
| ГД-2026-009-АИ.В19 | Визуализация. Интерьер: Гостиная-столовая (пом. 3), стена Б | |
| ГД-2026-009-АИ.В20 | Визуализация. Интерьер: Гостиная-столовая (пом. 3), стена В | |
| ГД-2026-009-АИ.В21 | Визуализация. Интерьер: Гостиная-столовая (пом. 3), стена Г | |
| ГД-2026-009-АИ.В22 | Визуализация. Интерьер: Кабинет-библиотека (пом. 1), стена А | |
| ГД-2026-009-АИ.В23 | Визуализация. Интерьер: Кабинет-библиотека (пом. 1), стена Б | |
| ГД-2026-009-АИ.В24 | Визуализация. Интерьер: Кабинет-библиотека (пом. 1), стена Г | |
| ГД-2026-009-АИ.В25 | Визуализация. Интерьер: Постирочная (пом. 7), общий вид | |

**Допущения и предложения на листе**

Основа листа: размеры сняты со скана обмерного плана KV оформление (см): часть подписей не читается, помещения выровнены по читаемым размерам; контрольный обмер не выполнен (К-1); высота потолка 2650 мм принята по отметкам обмера (Н = 2,50…2,66 м, ригель 2,28 м) — уточнить при обмере (К-2); толщины стен 300 / 120 мм приняты, межквартирная стена и колонны — по скану, не замерены (К-1); разрешённая мощность 15 кВт принята по типовым ТУ; при объединении двух квартир — переоформление ТУ (К-4); подрайон климата не задан — принят не северный (жилые от 2,5 м) (К-8).

См. лист открытых вопросов (лист 6, записи К-1, К-2, К-4, К-8).

| Изм. | Кол.уч | Лист | № док. | Подп. | Дата |
|---|---|---|---|---|---|
| Разраб. | | Кырлан А.С. | | | 04.11.26 |
| Пров. | | | | | |
| ГИП | | | | | |
| | | | | | |
| Н. контр. | | | | | |
| Утв. | | | | | |

**ГД-2026-009-АИ**

Квартира 103 м²

Общая площадь 100,72* м² · * размеры со скана, не замерены (реестр — л. 6, 7, К-1)

Дизайн-проект интерьера

| Стадия | Лист | Листов |
|---|---|---|
| РП | 4 | 120 |

**Общие данные**

М б/м

**Кырлан Александр Сергеевич**

выпуск 04.11.2026 № 35b47f1c2a · стр. 4 из 130

# Общие данные

Комплект ГД-2026-009-АИ · лист 4 общих данных (продолжение)

## Состав дизайн-проекта

| Раздел | Состав | Листы |
|---|---|---|
| Обложка | Дизайн-проект интерьера; Квартира 103 м²; автор проекта — Кырлан Александр Сергеевич | 1 с. |
| Концепция | Стиль Мид-сенчури 65 % + Ар-деко 35 %: концепция интерьера, палитра и материалы (колерная карта — лист 57) | л. 18 |
| Визуализации | 25 изобр.: Вид сверху (3D): планировка с мебелью, текстилем и декором; Ванная, стена Б; Ванная, стена В; Ванная, стена Г; Ванная мастер, общий вид; Спальня 2, стена А; Спальня 2, стена Б; Спальня 2, стена Г; Спальня мастер, стена А; Спальня мастер, стена Б; Спальня мастер, стена В; Спальня мастер, стена Г; Коридор, стена Б; Прихожая-холл, стена А; Прихожая-холл, стена Б; Кухня, стена Б; Кухня, стена В; Гостиная-столовая, стена А; Гостиная-столовая, стена Б; Гостиная-столовая, стена В; Гостиная-столовая, стена Г; Кабинет-библиотека, стена А; Кабинет-библиотека, стена Б; Кабинет-библиотека, стена Г; Постирочная, общий вид | В1–В25 |
| Рабочие чертежи | планы, развёртки, узлы (развёртки и узлы — листы 38–41, 79–82, 92, 94, 95, 98, 99, 108, 110, 113) | л. 1–120 |
| Спецификации и ведомости | оборудование, изделия, отделка, электроточки | л. 17, 20–22, 26, 27, 42, 54–60, 64, 65, 114–118 |

## Условные обозначения

- контрольный отрезок 1000 мм натуры: по нему проверяют печать 1:1
- отметка уровня, м: ±0,000 — чистый пол жилых помещений
- (А) марка развёртки: буква стены, стрелка — взгляд
- (О1) марка отделки по реестру отделки альбома
- выноска узла: над полкой — узел, под полкой — лист

## Общие указания

1. Рабочие чертежи интерьера разработаны на основании задания на проектирование и обмерного плана (лист 14). Объект: Квартира 103 м²; автор проекта — Кырлан Александр Сергеевич; общая площадь 100,72 м², жилая 64,79 м², помещений 11.
2. Рабочие чертежи выполнены в соответствии с заданием на проектирование и нормативными документами, перечисленными в п. 4.
3. Открытые вопросы, принятые допущения и конфликты между разделами, не снятые к выпуску комплекта, сведены в таблицы на листах 6, 7. До ответа по пункту таблицы показанное на указанном там листе — допущение, а не утверждённое решение: комплект по этим листам предварительный.
4. Нормативные документы, на которые есть ссылки в листах комплекта: ГОСТ Р 21.101-2026; ГОСТ 21.501-2018; ГОСТ 2.302-68; ГОСТ 2.303-68; ГОСТ 2.304-81; ГОСТ 2.307-2011; СП 54.13330.2022; СП 71.13330.2017; СП 73.13330.2016; ПУЭ (7-е изд.), гл. 1.8, 7.1; ГОСТ Р 50571.7.701-2024; СанПиН 1.2.3685-21; ГОСТ 2.702; ГОСТ 2.755; ГОСТ 21.110-2013; ГОСТ 21.601; ГОСТ 13996-2019; ГОСТ 31173-2016; ГОСТ 31565-2012; ГОСТ 32414-2013; ГОСТ 32415-2013; ГОСТ Р 56387-2018; ГОСТ Р 56926; СП 29.13330.2011; СП 30.13330.2020; СП 51.13330.2011; СП 131.13330. Документы из ведомости ссылочных документов здесь не повторяются.
5. За отметку ±0,000 принят уровень чистого пола жилых помещений квартиры (относительная отметка; абсолютная — по проекту дома). Отметка чистого пола мокрых помещений — −0,015. Размеры — в миллиметрах, отметки — в метрах, площади — в м²; высоты установки Н от чистого пола своего помещения до оси изделия.
6. Несущие конструкции, общедомовые стояки, вентиляционные каналы и инженерные сети дома настоящим комплектом не изменяются. Работы, затрагивающие их (проём или штраба в несущей стене, перенос стояка, врезка в вентканал, расширение мокрой зоны), выполняются только по отдельному проекту, к которому прилагается техническое заключение о допустимости и безопасности работ, выданное автором проекта дома или организацией с допуском на обследование, и который согласован в установленном порядке (Жилищный кодекс РФ, ст. 25–29).
7. Трассы инженерных сетей на листах — принципиальные. Расчёты электрических нагрузок и токов КЗ, гидравлики, воздухообмена, освещённости и нагрузок на перекрытие выполняются в проектах ЭОМ, ВК, ОВ и КР организацией с допуском СРО; фактические трассы до закрытия отделкой фиксируются исполнительными схемами.
8. Стиль интерьера — Мид-сенчури 65 % + Ар-деко 35 %. Палитра проекта: основной 60 % — Farrow & Ball No. 291 «School House White — тёплый меловой белый», NCS S 0502-Y «Белый с лёгкой желтизной»; дополнительный 30 % — Farrow & Ball No. 298 «Bancha — оливковый середины века», Farrow & Ball No. 289 «Inchyra Blue — тёмный сине-серый», Farrow & Ball No. 255 «Tanner's Brown — тёмный шоколад»; акцент 10 % — NCS S 2050-Y20R «Горчичный», NCS S 3050-Y70R «Терракотовый / жжёный оранжевый», NCS S 5030-B10G «Тил», NCS S 5040-B90G «Изумрудный». Коды цвета — по веерам производителей; цвет утверждается по выкрасу на объекте при освещении проекта.
9. Площади поверхностей — по чистым граням стен до отделки: стены = периметр × высоту от чистого пола помещения до низа потолка минус проёмы (облицовка плиткой — до верха облицовки); плинтус = периметр минус дверные проёмы; пол и потолок — по площади помещения. Количество плиток — по раскладке. Способ один для всех листов комплекта (ведомость отделки, колерная карта, раскладка плитки, развёртки).
10. Марки: стены помещения на всех листах — А (верхняя по плану), Б (правая), В (нижняя), Г (левая); марка отделки О — одна на весь альбом; реестр марок отделки (с позициями колерной карты той же отделки) и марки позиций по видам — на листе 78.
11. Развёртки стен выполнены по всем помещениям для стен с электроточками, мебелью, декором и отделкой: санузлы и кухонный фронт — в М 1:25, остальные стены — в М 1:25; расположение развёрток и узлов — на листе 79, узлы — на листе 113.
12. Перечень скрытых работ, на которые составляются акты освидетельствования (форма по приказу Минстроя России № 344/пр): гидроизоляция пола и стен мокрых помещений (с тестом проливом); стяжка пола (толщина, прочность, влажность основания); скрытая электропроводка (за потолком и в штробах стен; условия штробления — в следующем пункте); трубопроводы водоснабжения и канализации до закрытия (опрессовка, уклоны); закладные и усиления под подвесные приборы, мебель и тяжёлый декор, рамы инсталляций; короба дверей скрытого монтажа до штукатурки; каркасы ГКЛ потолков, коробов и перегородок до обшивки.
13. Скрытая электропроводка: за потолком и в штробах стен. Штробы в стенах выполняются только после технического заключения о несущих конструкциях; до заключения несущие стены не определены, и все стены считаются несущими; объём штроб — в ведомости объёмов работ, строка «Штробы в стенах» (вертикальные спуски; объём не меньше фактического, горизонтальные трассы — по исполнительной схеме).
14. Критерии приёмки: допуски отделочных покрытий — по СП 71.13330.2017; испытания систем водоснабжения и канализации — по СП 73.13330.2016 до закрытия трасс; приёмо-сдаточные испытания электроустановки — по ПУЭ, гл. 1.8, с протоколом электролаборатории.
15. Осознанные отступления от ГОСТ Р 21.101-2026, принятые в комплекте: номер листа и число листов («Листов») указаны на каждом листе; на масштабных листах в основной надписи указан фактический масштаб и дан контрольный отрезок 1000 мм; развёртки стен выполнены в М 1:25 (ГОСТ 21.507-81 — 1:50…1:500) ради читаемости привязок; размерные числа и марки элементов (Д-1, ОК-1, О6) кеглем 2,5 мм, номера помещений — в кружке Ø 8 мм (канон — 3,5 мм и Ø 12 мм): так насыщенные листы А3 читаются без наложений надписей.
16. Графы «Пров.», «Н. контр.», «Утв.» основной надписи заполняются при согласовании комплекта с заказчиком; до согласования комплект подписывает автор проекта (графа «Разраб.»).

**Допущения и предложения на листе**

Основа листа: размеры сняты со скана обмерного плана KV оформление (см): часть подписей не читается, помещения выровнены по читаемым размерам; контрольный обмер не выполнен (К-1); высота потолка 2650 мм принята по отметкам обмера (Н = 2,50…2,66 м, ригель 2,28 м) — уточнить при обмере (К-2); толщины стен 300 / 120 мм приняты, межквартирная стена и колонны — по скану, не замерены (К-1); разрешённая мощность 15 кВт принята по типовым ТУ; при объединении двух квартир — переоформление ТУ (К-4); подрайон климата не задан — принят не северный (жилые от 2,5 м) (К-8).

См. лист открытых вопросов (лист 6, записи К-1, К-2, К-4, К-8).

| Изм. | Кол.уч | Лист | № док. | Подп. | Дата | ГД-2026-009-АИ | | |
|---|---|---|---|---|---|---|---|---|
| | | | | | | Квартира 103 м² | | |
| | | | | | | Общая площадь 100,72* м² · * размеры со скана, не замерены (реестр — л. 6, 7, К-1) | | |
| Разраб. | | Кырлан А.С. | | | 04.11.26 | Дизайн-проект интерьера | Стадия: РП | Лист: 5 / Листов: 120 |
| Пров. | | | | | | | | |
| ГИП | | | | | | | | |
| Н. контр. | | | | | | **Общие данные** М б/м | **Кырлан Александр Сергеевич** | |
| Утв. | | | | | | | | |

выпуск 04.11.2026 № 35b47f1c2a · стр. 5 из 130

# Открытые вопросы, принятые допущения и конфликты. Лист 1 из 2

**ПРЕДВАРИТЕЛЬНО · не для производства работ · открыто пунктов: 8 (реестр — л. 6, 7)**

Сводка по реестрам координации (стартовое совещание 18.10.2026)

Комплект предварительный по пунктам этих таблиц. Пока по пункту нет ответа или решения, показанное на указанном листе — допущение проектировщика, а не утверждённое решение.
Сводка: открытых вопросов — 7 (из них ждут факта объекта — 4: контрольного обмера, обследования или документа); изменений в реестре — 1, из них без подписи — 1.
Пункты, ответ на которые лежит на объекте, а не за столом проектировщика (графа «Вид», строка «Ждёт»), собраны на листе «Задание на контрольный обмер и обследование» (листы 8–10): что и где замерить, с какой точностью и чем подтвердить. Пункты, ждущие решения человека, на объекте не закрываются.

## Открытые вопросы и принятые допущения

| № | Формулировка | Вид | Кто решает | Если решения нет | Лист, где это проявляется |
|---|---|---|---|---|---|
| К-1 | Размеры сняты со скана обмерного плана KV оформление (в см): часть подписей не читается, помещения выровнены по читаемым размерам. До заказа мебели, дверей и материалов нужен контрольный обмер. | Отсутствует<br>Ждёт: обмера | Архитектор-планировщик | размеры на листах — по плану заказчика, уточняются по месту; мебель на заказ и материалы по ним не заказывать | л. 14 — Обмерный план<br>л. 19 — План расстановки мебели |
| К-2 | Высота потолка принята 2650 мм по отметкам обмера (Н = 2,50…2,66 м); под ригелем 2,28 м — уточнить. | Отсутствует | Архитектор-планировщик | высоты на развёртках и потолки — от 2650 мм, уточнить при обмере | л. 14 — Обмерный план<br>л. 45 — План потолков |
| К-4 | Разрешённая мощность объединённой квартиры по ТУ неизвестна, принята 15 кВт; при объединении двух квартир ТУ переоформляются. | Отсутствует | Инженер-электрик | щит и группы рассчитаны на 15 кВт; при меньших ТУ пересчёт | л. 28 — Однолинейная схема щита<br>л. 23 — План розеток и электровыводов |
| К-5 | Объединение двух квартир в одну (проём в межквартирной стене между гостиной и коридором правой квартиры, вход — один из тамбура, второй вход закрывается; правая кухня — постирочная) — предложение проектировщика. Межквартирная стена, колонны и ригель — несущие или нет, неизвестно (на обмере отмечены «несущие колонны» и «ригель перекрытия»): нужны поэтажный план БТИ, техзаключение и согласование перепланировки (ЖК РФ ст. 25–29). | Отсутствует<br>Ждёт: документа | Архитектор-планировщик | проём и перегородки — предложение, к строительству не выдаются; мокрые зоны и кухня оставлены на местах обмера | л. 14 — Обмерный план |
| К-6 | Ванная мастер (пом. 11): стояки Ст К1-3 Ø110, Ст В1-3, Ст Т3-3 по данным стоят в углу стен В и Г (оси ≈ 90–240 мм от стены Г, 150–280 мм от стены В) — внутри габарита душевого поддона См1 800 × 800 у стены В, а душ со стеклоблочной перегородкой по плану сохраняется. Поддон на стояки не встанет, короба (зазор 50 мм) и люка 300 × 400 к арматуре нет. Положение стояков снято со скана обмера (К-1), отдельно не замерялось. Нужен контрольный обмер угла: оси стояков от двух стен, перегородка из стеклоблоков. Затем решить: (а) короб стояков в углу ≈ 310 × 350 с люком, поддон 800 × 800 сдвинуть вдоль стены В от короба, стеклоблочную перегородку разобрать и выложить заново по новому поддону; (б) поддон меньше, вне короба (по месту после обмера); (в) душ с трапом без поддона по обходу короба. | Спорно<br>Ждёт: обмера, затем решения | Инженер ВК (вода, канализация) | душевую зону См1, поддон и перегородку не выполнять; выводы См1 и короб стояков — после обмера | л. 33 — План выводов сантехники<br>л. 34 — Схема разводки водопровода и канализации<br>л. 14 — Обмерный план |
| К-7 | Унитаз подвесной Сн2 (пом. 6 «Ванная»), выпуск К1-2 Ø110: трасса до Ст К1-1 (1,91 м) идёт под дверным проёмом Д-5 — короб над полом там не поставить. Решить: (а) прибор ближе к стояку Ст К1-1 (без прохода под проёмом); (б) выпуск в полу с подъёмом пола помещения на 160 мм; (в) насосная установка (КНС) у прибора — по паспорту, требует согласования. Решение меняет санузел (высоты, раскладку плитки) — за автором с заказчиком. | Спорно<br>Ждёт: решения | Инженер ВК (вода, канализация) | выпуск К1-2 и прибор Сн2 не выполнять до решения; остальное — по листам | л. 34 — Схема разводки водопровода и канализации<br>л. 33 — План выводов сантехники |
| К-8 | Климатический подрайон (СП 131.13330) не задан: принят не северный — жилые комнаты и кухня под потолком от 2,5 м (СП 54, п. 5.12); в IA, IБ, IГ, IД, IVA — от 2,7 м. | Отсутствует<br>Ждёт: документа | Архитектор-планировщик | отметки потолков жилых — по 2,5 м; при северном подрайоне уровни ниже 2,7 м пересчитать до заказа каркаса | л. 45 — План потолков |

## Изменения проекта после выпуска листов (реестр изменений)

| № | Дата | Лист | Было | Стало | Кто решил, подпись |
|---|---|---|---|---|---|
| ИЗ-1 | 30.10.2026 | л. 28 — Однолинейная схема щита<br>л. 23 — План розеток и электровыводов<br>л. 51 — Раскладка плитки. Ванная. Развёртки стен<br>л. 16 — План дверей<br>л. 59 — Спецификация отделочных материалов<br>л. 33 — План выводов сантехники | Фены Р8, Р33 и полотенцесушители В6, В7 сидели на гр. 13 «посудомоечная машина», стиральная машина Р50 — на гр. 12 «духовой шкаф»; групп 7 и 8 в щите не было. Два вывода печатались «ЭВ4» (духовой шкаф «ЭВ4» на кухне и вентилятор «В4» ванной). Окно 2 спальни мастер (смещение 3500, 1300) выходило за стену Б (3830). Пол ванных и плинтус МДФ — без артикула. Стояки Ст К1-3/В1-3/Т3-3 без признака допущения. | Группы 7 (санузлы: фены, полотенцесушители, УЗО 10 мА) и 8 (стиральная машина постирочной) добавлены, точки переназначены. Выводы кухни — В1 (варочная), В2 (духовой шкаф), печать ЭВ1/ЭВ2 — марки на листах уникальны. Окно 2 — стена Б части 1, смещение 100, знак «*» (К-1). Пол ванных — Marvel Travertine Sand Cross 60×60 AFUL, плинтус — Ultrawood Base 5340 83×15. Стояки ванной мастер — assumed, К-6; остаётся до обмера. | Не утверждено: подписи нет. решение исполнителя; на утверждение А. С. Кырлана |

| Изм. | Кол.уч | Лист | № док. | Подп. | Дата |
|---|---|---|---|---|---|
| Разраб. | | Кырлан А.С. | | | 04.11.26 |
| Пров. | | | | | |
| ГИП | | | | | |
| | | | | | |
| Н. контр. | | | | | |
| Утв. | | | | | |

**ГД-2026-009-АИ**

Квартира 103 м²

Общая площадь 100,72* м² · * размеры со скана, не замерены (реестр — л. 6, 7, К-1)

Дизайн-проект интерьера

| Стадия | Лист | Листов |
|---|---|---|
| РП | 6 | 120 |

**Открытые вопросы, принятые допущения и конфликты. Лист 1 из 2**
М б/м

**Кырлан Александр Сергеевич**

# Открытые вопросы, принятые допущения и конфликты. Лист 2 из 2

Сводка по реестрам координации (стартовое совещание 18.10.2026)

**ПРЕДВАРИТЕЛЬНО · не для производства работ · открыто пунктов: 8 (реестр — л. 6, 7)**

### Примечания

1. Номера листов — по ведомости рабочих чертежей комплекта (лист «Общие данные»).
2. Графа «Если решения нет» показывает состояние решения на листах; влияние на сроки и стоимость по пунктам не оценивалось.
3. Пункт, по которому принято решение, при следующем выпуске комплекта из таблиц исключается.

**Допущения и предложения на листе**

Основа листа: размеры сняты со скана обмерного плана KV оформление (см): часть подписей не читается, помещения выровнены по читаемым размерам; контрольный обмер не выполнен (К-1); высота потолка 2650 мм принята по отметкам обмера (Н = 2,50…2,66 м, ригель 2,28 м) — уточнить при обмере (К-2); толщины стен 300 / 120 мм приняты, межквартирная стена и колонны — по скану, не замерены (К-1); разрешённая мощность 15 кВт принята по типовым ТУ; при объединении двух квартир — переоформление ТУ (К-4); подрайон климата не задан — принят не северный (жилые от 2,5 м) (К-8).

См. лист открытых вопросов (лист 6, записи К-1, К-2, К-4, К-8).

| Изм. | Кол.уч | Лист | № док. | Подп. | Дата |
|---|---|---|---|---|---|
| Разраб. | | Кырлан А.С. | | | 04.11.26 |
| Пров. | | | | | |
| ГИП | | | | | |
| | | | | | |
| Н. контр. | | | | | |
| Утв. | | | | | |

**ГД-2026-009-АИ**

Квартира 103 м²

Общая площадь 100,72* м² · * размеры со скана, не замерены (реестр — л. 6, 7, К-1)

Дизайн-проект интерьера

| Стадия | Лист | Листов |
|---|---|---|
| РП | 7 | 120 |

**Открытые вопросы, принятые допущения и конфликты. Лист 2 из 2**

М б/м

**Кырлан Александр Сергеевич**

выпуск 04.11.2026 № 35b47f1c2a · стр. 7 из 130

# Задание на контрольный обмер и обследование. Лист 1 из 3

**ПРЕДВАРИТЕЛЬНО · не для производства работ · открыто пунктов: 8 (реестр — л. 6, 7)**

Что замерить, вскрыть и получить до заказа материалов и изделий

Задание собрано из открытых вопросов, ответ на которые лежит на объекте или в документах, а не за столом проектировщика. Пока факт не получен, размер, материал или положение на листах — допущение (знак «*»), а не замер.
Сводка: на объекте — 9 (до демонтажа — 7; после демонтажа — 2); документом и при закупке — 3; из допущений в данных и на листах — 10, из них без вопроса в реестре — 4. Закрываются вопросы: К-1, К-2, К-4–К-6, К-8 (6). Вопросы, ждущие решения человека, задание не закрывает — они решаются по реестру открытых вопросов.

## Условия проведения

| Порядок работ | Приёмы и точность | Кто присутствует | Если факт не совпал с проектом |
|---|---|---|---|
| 1. До демонтажа — существующее состояние: контур, диагонали, высоты, проёмы, оси стояков, ниши и конструкции, которые видны.<br>2. После демонтажа, до черновых работ — то, что закрывали отделка и короба: основание стен, фактические толщины, углы, узлы.<br>3. Документы и данные закупки — не на объекте: к сроку из последней таблицы, от них зависят привязки и заказ.<br>Что заказывается по размеру из задания, до закрытия пункта не заказывают: сроки изготовления — по графику закупок прораба. | Обход по часовой стрелке от входа: стены, проёмы, потолок, коммуникации (стояки, щиток, вентканалы), особенности (ниши, короба, выступы).<br>Размеры записывают в мм; сумма участков равна общему размеру, при цепочке длиннее трёх участков ставят проверочный (общий) размер.<br>Диагонали каждого помещения; если две диагонали различаются на 5 мм и больше, разницу подписывают на плане.<br>Потолок — в нескольких точках: центр, углы, у проёмов. Проём — ширина, высота, глубина откоса, привязка к ближайшим углам, высота подоконника.<br>Допустимая погрешность прибора — 2–3 мм на метр; размеры округляют кратно 5 мм; два контрольных промера одного размера не должны расходиться более чем на 2 %. Допуск по пункту — в графе «Точность».<br>План БТИ обмер не заменяет. | Прораб (отвечает за проведение) — назначает день и порядок обхода, открывает объект и освобождает помещения, ведёт это задание и реестр изменений.<br>Архитектор — выполняет обмер, составляет акт контрольного обмера и подписывает результаты по размерам и конструкциям.<br>Владельцы вопросов присутствуют при пунктах своего раздела или принимают результат до заказа: Инженер ВК (вода, канализация) — К-6; Инженер-электрик — К-4; позиции О-1; Инженер ОВ — позиции О-2; Отделочник — позиции О-8, О-9.<br>Заказчик или его представитель — передаёт документы (план БТИ, проект дома, технические условия, паспорта), подписывает акт. Проектных решений на обмере не принимают: обмер даёт факт, решения — по реестру открытых вопросов (листы 6–7). | 1. В пределах допуска пункта — принимается измеренное значение, лист перевыпускается, знак «*» снимается.<br>2. Больше допуска или контрольные промеры расходятся более чем на 2 % — промер повторяют; не подтвердилось — запись в реестр изменений (дата, лист, было, стало, кто решил, подпись), работы в этом месте не начинают.<br>3. Затронуты несущая стена, стояк, вентканал или мокрая зона — сразу владельцу раздела и ГИПу (главному инженеру проекта); между разделами не больше двух кругов, затем решает ГИП.<br>4. На объекте устно ничего не согласуется: каждое решение — записью в реестр с подписью. |

## Этап 1. До демонтажа

| № | Где | Способ | Что сделать | Кто выполняет | Точность | Что пересчитается в альбоме | Чем подтверждается | Закрывает вопросы реестра |
|---|---|---|---|---|---|---|---|---|
| О-1 | Вход в квартиру или лестничная клетка; место щита на плане | Обмер | Существующий щиток и счётчик электроэнергии: место и габарит ниши, состояние ввода, марка и сечение вводного кабеля, наличие вводного автомата и УЗО, пломбы. | Архитектор | ±5 мм | Ниша и место щита на листах; вводной кабель и аппараты на однолинейной схеме; расстояния до первых групп.<br>Листы:<br>л. 28 — Однолинейная схема щита | акт контрольного обмера; фото с рулеткой и привязкой к стене или углу | Вопроса в реестре нет: Альбом принимает щит и ввод без осмотра.<br>Результат принимает: Инженер-электрик |
| О-2 | Кабинет-библиотека (пом. 1), Гостиная-столовая (пом. 3), Кухня (пом. 5), Спальня 2 (пом. 8), Спальня мастер (пом. 10); у окон | Обмер | Положение стояков отопления (подающий и обратный) от граней стен, диаметры, наличие запорной арматуры; существующие радиаторы: число секций, межосевое расстояние, подводки. В данных стояков отопления нет — лист отопления выводит их условно у откоса окна, радиаторы — «принципиально, по расчёту». | Архитектор | ±5 мм | План отопления: места стояков и подводок, привязки радиаторов; подбор радиаторов по теплотехническому расчёту; радиаторы и узлы подключения в ВОР и спецификации.<br>Листы:<br>л. 32 — План отопления | акт контрольного обмера; фото с рулеткой и привязкой к стене или углу | Вопроса в реестре нет: Альбом принимает положение стояков и радиаторов отопления без обмера.<br>Результат принимает: Инженер ОВ |
| О-3 | все помещения | Обмер | Контрольный обмер всех помещений: стороны, диагонали, проёмы, высота потолка. | исполнитель | ±5 мм; диагонали — разница от 5 мм подписывается | обмерный и монтажный планы, развёртки, мебель на заказ<br>Листы:<br>л. 14 — Обмерный план<br>л. 19 — План расстановки мебели | акт контрольного обмера | К-1<br>Результат принимает: Архитектор |
| О-4 | Все помещения квартиры | Обмер | Высота потолка в каждом помещении в нескольких точках: центр, углы, у проёмов. | Архитектор | ±5 мм | Вертикальные размеры альбома: развёртки, шкафы, плитка, объёмы работ.<br>Листы:<br>л. 2–5 — Общие данные | акт контрольного обмера | К-2<br>Результат принимает: Архитектор |
| О-5 | По месту | Обмер | Подтвердить на объекте принятое: подрайон климата не задан — принят не северный (жилые от 2,5 м) | Архитектор | ±5 мм | Листы, где используется принятая величина.<br>Листы:<br>л. 2–5 — Общие данные | акт контрольного обмера | К-8<br>Результат принимает: Архитектор |

**Допущения и предложения на листе**
Основа листа: размеры сняты со скана обмерного плана KV оформление (см): часть подписей не читается, помещения выровнены по читаемым размерам; контрольный обмер не выполнен (К-1); высота потолка 2650 мм принята по отметкам обмера (Н = 2,50…2,66 м, ригель 2,28 м) — уточнить при обмере (К-2); толщины стен 300 / 120 мм приняты, межквартирная стена и колонны — по скану, не замерены (К-1); разрешённая мощность 15 кВт принята по типовым ТУ; при объединении двух квартир — переоформление ТУ (К-4); подрайон климата не задан — принят не северный (жилые от 2,5 м) (К-8).
См. лист открытых вопросов (лист 6, записи К-1, К-2, К-4, К-8).

| Изм. | Кол.уч | Лист | № док. | Подп. | Дата |
|---|---|---|---|---|---|
| Разраб. | | Кырлан А.С. | | | 04.11.26 |
| Пров. | | | | | |
| ГИП | | | | | |
| | | | | | |
| Н. контр. | | | | | |
| Утв. | | | | | |

**ГД-2026-009-АИ**

Квартира 103 м²

Общая площадь 100,72* м² · * размеры со скана, не замерены (реестр — л. 6, 7, К-1)

Дизайн-проект интерьера

| Стадия | Лист | Листов |
|---|---|---|
| РП | 8 | 120 |

**Задание на контрольный обмер и обследование.**
**Лист 1 из 3**
М б/м

**Кырлан Александр Сергеевич**

выпуск 04.11.2026 № 35b47f1c2a · стр. 8 из 130

# Задание на контрольный обмер и обследование. Лист 2 из 3

Что замерить, вскрыть и получить до заказа материалов и изделий

### Этап 1. До демонтажа (продолжение)

| № | Где | Способ | Что сделать | Кто выполняет | Точность | Что пересчитается в альбоме | Чем подтверждается | Закрывает вопросы реестра |
|---|---|---|---|---|---|---|---|---|
| О-6 | Спальня мастер (пом. 10): окно пом. 10, стена Б | Обмер | Окно пом. 10, стена Б: положение (привязки к ближайшим углам), ширина, высота, высота подоконника, глубина откоса. Принято в проекте: Окно 1300 при смещение 3500 на стене Б основной части (длина 3830) выходило за стену на 970 мм. Отнесено к стене Б части 1 (у 6300…7800): смещение 100 положение со скана, не замерено.. | Архитектор | ±5 мм | Проёмы на обмерном плане и в ведомости проёмов; откосы и оконные работы в ВОР; привязки мебели и выводов к проёмам.<br>Листы:<br>л. 14 — Обмерный план<br>л. 17 — Ведомость заполнения проёмов | акт контрольного обмера; фото с рулеткой и привязкой к стене или углу | К-1<br>Результат принимает: Архитектор |
| О-7 | Ванная мастер (пом. 11): Ст К1-3*, Ст В1-3, Ст Т3-3*; наличие стояка ГВС, арматуры и счётчиков — по всей квартире | Обмер | Положение стояков Ст К1-3*, Ст В1-3*, Ст Т3-3*: привязка осей от граней стен, диаметры, размеры короба и люков. Стояк горячей воды Т3 в данных не задан, на листах ВК принят рядом с стояком холодной воды: выяснить, есть ли он в доме, и где. Отключающая арматура и счётчики воды на вводах: положение, тип, пломбы управляющей компании. Сверить до разметки выводов. | Архитектор | ±5 мм | Привязки выводов воды и канализации на планах выводов и разводки; расстояние розеток до стояка; места люков 300 × 400 мм; трассы Т3 и полотенцесушители (водяной или электрический); узлы ввода в спецификации ВК (краны, фильтры, счётчики).<br>короб и люк стояков, поддон См1, выводы душа, раскладка плитки ванной мастер<br>Листы:<br>л. 33 — План выводов сантехники<br>л. 34 — Схема разводки водопровода и канализации<br>л. 14 — Обмерный план | акт контрольного обмера; фото с рулеткой и привязкой к стене или углу | К-6<br>Результат принимает: Инженер ВК (вода, канализация) |

### Этап 2. После демонтажа, до черновых работ

| № | Где | Способ | Что сделать | Кто выполняет | Точность | Что пересчитается в альбоме | Чем подтверждается | Закрывает вопросы реестра |
|---|---|---|---|---|---|---|---|---|
| О-8 | Кабинет-библиотека (пом. 1), Кладовая (пом. 2), Гостиная-столовая (пом. 3), Прихожая-холл (пом. 4), Кухня (пом. 5), Ванная (пом. 6), Постирочная (пом. 7), Спальня 2 (пом. 8), Коридор (пом. 9), Спальня мастер (пом. 10), Ванная мастер (пом. 11) | Обмер | Нивелировка плиты перекрытия и существующего пола после демонтажа покрытий: отметки в углах и по сетке, перепады по помещению, уклоны, отметки порогов (чистый пол в мокрых зонах принят -15 мм, 0 мм). Принятая толщина стяжки 33 мм, 47 мм, 49 мм, 50 мм и отметка чистого пола — расчётные, не от замера плиты. | Архитектор | ±5 мм по отметке; ровность просвет под 2-метровой рейкой, горизонталь против 0,2 % длины помещения | Толщина стяжки и отметка чистого пола; уклоны к трапам и пороги; выпуски К1 относительно чистого пола (план разводки); объёмы стяжки и смеси в ВОР и спецификации.<br>Листы:<br>л. 49, 53 — План полов<br>л. 34 — Схема разводки водопровода и канализации | акт контрольного обмера | Вопроса в реестре нет: Альбом принимает отметки плиты и толщину пирога пола без нивелировки.<br>Результат принимает: Отделочник |
| О-9 | Кабинет-библиотека (пом. 1), Кладовая (пом. 2), Гостиная-столовая (пом. 3), Прихожая-холл (пом. 4), Кухня (пом. 5), Ванная (пом. 6), Постирочная (пом. 7), Спальня 2 (пом. 8), Коридор (пом. 9), Спальня мастер (пом. 10), Ванная мастер (пом. 11) | Обмер | Вертикаль и плоскостность стен: отклонение от вертикали по высоте стены (отвес или лазерный уровень), просвет под правилом 2 м, кривизна углов. Нужно там, где от стены зависит изделие: облицовка плиткой (пом. 6, 11), штукатурка и окраска (пом. 1, 2, 3, 4, 5, 6, 7, 8, 9, 10, 11), встроенная мебель и кухня (пом. 4, 5, 8, 10). | Архитектор | до 1 мм на 2 м (правило и клиновой щуп); вертикаль — мм на высоту стены, отклонения подписываются на плане | Толщина штукатурки и расход смеси в ВОР и спецификации; раскладка плитки (подрезка у стен); зазоры и крепление встроенной мебели и кухни.<br>Листы:<br>л. 49–52 — Раскладка плитки<br>л. 54–56 — Ведомость отделки помещений | акт контрольного обмера | Вопроса в реестре нет: Альбом принимает стены ровными и вертикальными без замера.<br>Результат принимает: Отделочник |

**Допущения и предложения на листе**

Основа листа: размеры сняты со скана обмерного плана KV оформление (см): часть подписей не читается, помещения выровнены по читаемым размерам; контрольный обмер не выполнен (К-1); высота потолка 2650 мм принята по отметкам обмера (Н = 2,50…2,66 м, ригель 2,28 м) — уточнить при обмере (К-2); толщины стен 300 / 120 мм приняты, межквартирная стена и колонны — по скану, не замерены (К-1); разрешённая мощность 15 кВт принята по типовым ТУ; при объединении двух квартир — переоформление ТУ (К-4); подрайон климата не задан — принят не северный (жилые от 2,5 м) (К-8).

Знак «*» — принято, не замерено и не подтверждено (замерить на объекте): К-6: Ст К1-3, Ст В1-3, Ст Т3-3 — положение снято со скана обмера, отдельно не замерялось; ось внутри габарита поддона См1 — обмер угла по К-6.

См. лист открытых вопросов (лист 6, записи К-1, К-2, К-4, К-6, К-8).

| Изм. | Кол.уч | Лист | № док. | Подп. | Дата |
|---|---|---|---|---|---|
| Разраб. | | Кырлан А.С. | | | 04.11.26 |
| Пров. | | | | | |
| ГИП | | | | | |
| | | | | | |
| Н. контр. | | | | | |
| Утв. | | | | | |

**ГД-2026-009-АИ**

Квартира 103 м²

Общая площадь 100,72* м² · * размеры со скана, не замерены (реестр — л. 6, 7, К-1)

Дизайн-проект интерьера

| Стадия | Лист | Листов |
|---|---|---|
| РП | 9 | 120 |

**Задание на контрольный обмер и обследование.**
**Лист 2 из 3**
М б/м

**Кырлан Александр Сергеевич**

# Задание на контрольный обмер и обследование. Лист 3 из 3

**ПРЕДВАРИТЕЛЬНО · не для производства работ · открыто пунктов: 8 (реестр — л. 6, 7)**

Что замерить, вскрыть и получить до заказа материалов и изделий

### Документы и данные закупки (не на объекте)

| № | У кого, откуда | Способ | Что получить | К какому сроку | Что пересчитается в альбоме | Чем подтверждается | Закрывает вопросы реестра |
|---|---|---|---|---|---|---|---|
| О-10 | Заказчик; организация, выдавшая технические условия | Документ | Технические условия на присоединение: разрешённая мощность. | До утверждения однолинейной схемы щита | Однолинейная схема щита: вводной аппарат и группы.<br>Листы:<br>л. 2–5 — Общие данные | копия документа | К-4<br>Результат принимает:<br>Инженер-электрик |
| О-11 | вся квартира | Документ | Поэтажный план БТИ и техническое заключение о несущих стенах. | до демонтажа и возведения перегородок | монтажный план, проёмы, развёртки<br>Листы:<br>л. 14 — Обмерный план | копия документа | К-5<br>Результат принимает: Архитектор |
| О-12 | адрес объекта, СП 131.13330 | Документ | Климатический подрайон по СП 131.13330 (по адресу объекта) | до заказа каркаса потолков | план потолков, разрезы, ведомость объёмов<br>Листы:<br>л. 45 — План потолков | копия документа | К-8<br>Результат принимает: Архитектор |

### Примечания

1. Подтверждение: акт контрольного обмера (дата, кто присутствовал, прибор, перечень промеров с результатами, подписи присутствующих); к акту — фото вскрытий и узлов и техническое заключение организации, выполнившей обследование.
2. Номера листов — по ведомости рабочих чертежей комплекта (лист «Общие данные»).
3. Пункт исключается из задания при следующем выпуске, когда акт подписан, значение внесено в проект и листы перевыпущены; знак «*» у величины снимается только замером.

**Допущения и предложения на листе**

Основа листа: размеры сняты со скана обмерного плана KV оформление (см): часть подписей не читается, помещения выровнены по читаемым размерам; контрольный обмер не выполнен (К-1); высота потолка 2650 мм принята по отметкам обмера (Н = 2,50…2,66 м, ригель 2,28 м) — уточнить при обмере (К-2); толщины стен 300 / 120 мм приняты, межквартирная стена и колонны — по скану, не замерены (К-1); разрешённая мощность 15 кВт принята по типовым ТУ; при объединении двух квартир — переоформление ТУ (К-4); подрайон климата не задан — принят не северный (жилые от 2,5 м) (К-8).

См. лист открытых вопросов (лист 6, записи К-1, К-2, К-4, К-8).

| Изм. | Кол.уч | Лист | № док. | Подп. | Дата |
|---|---|---|---|---|---|
| Разраб. | | Кырлан А.С. | | | 04.11.26 |
| Пров. | | | | | |
| ГИП | | | | | |
| | | | | | |
| Н. контр. | | | | | |
| Утв. | | | | | |

**ГД-2026-009-АИ**

Квартира 103 м²

Общая площадь 100,72* м² · * размеры со скана, не замерены (реестр — л. 6, 7, К-1)

Дизайн-проект интерьера

| Стадия | Лист | Листов |
|---|---|---|
| РП | 10 | 120 |

**Задание на контрольный обмер и обследование.**
**Лист 3 из 3**
М б/м

**Кырлан Александр Сергеевич**

# График закупок и работ. Лист 1 из 3

Что заказывать и когда не раньше чего: относительный порядок без дат; срок поставки — из данных или «не задан» с записью реестра

**ПРЕДВАРИТЕЛЬНО · не для производства работ · открыто пунктов: 8 (реестр — л. 6, 7)**

Лист не содержит дат: контрольного обмера, подписанных решений автора и договоров ещё нет, и любая дата была бы выдумана. Вместо календаря — порядок и условия: замер → решение и выбор изделия → заказ → срок поставки → работа, которую позиция блокирует.
Срок поставки печатается как срок, только если он задан в данных позиции. Нет — «срок поставки не задан» и ссылка на вопрос реестра о сроках; типовой диапазон практики стоит рядом как ориентир и заказывать по нему нельзя. Номера З-N и Р-N — строки этого листа, К-N — записи реестра открытых вопросов, О-N — позиции задания на контрольный обмер.

## Закупки: что заказывается, от чего зависит заказ и какую работу блокирует

| № | Позиция и где | 1. Замер до заказа | 2. Решение, выбор изделия, паспорт | 3. Условие заказа | 4. Срок поставки | 5. Блокирует работу | Закрывает вопросы реестра |
|---|---|---|---|---|---|---|---|
| З-1 | Двери скрытого монтажа с коробом под покраску в существующих проёмах: Д-2, Д-3, Д-4, Д-5, Д-6, Д-7, Д-8, Д-9 — 8 шт.<br>пом. 1, 2, 5, 6, 7, 8, 10, 11 | О-6: обмер: Спальня мастер (пом. 10): окно пом. 10, стена Б (К-1)<br>О-3: обмер: все помещения (К-1); до заказа мебели и дверей | | После 1 и 2 и после получения срока у поставщика (вопроса о сроках нет); дата заказа — когда срок известен, не позднее чем за срок до начала Р-5. | срок поставки не задан (записи реестра нет)<br>Ориентир практики (не срок поставщика): ≈ 30 дн. | Р-5 «штукатурка»: короб ставят до штукатурки (коробку ставят на черновой стадии; полотно навешивают после чистовой отделки стен) | К-1 |
| З-2 | Кухонный гарнитур по проекту кухни: модули Кх1, Кх2, Кх3, Кх4, Кх7, Кх5, Кх8**<br>пом. 5 | | | После 1 и 2 и после получения срока у поставщика (вопроса о сроках нет); дата заказа — когда срок известен, не позднее чем за срок до начала Р-15. | срок поставки не задан (записи реестра нет)<br>Ориентир практики (не срок поставщика): 4–8 нед. от замера | Р-15 «кухня и мебель»: замер кухни — по готовым стенам после штукатурки или плитки, до чистового пола; производство идёт параллельно со стяжкой и отделкой | |
| З-3 | Встраиваемая техника кухни: Кх2 посудомоечная машина, Кх4 oven, Кх5 холодильник, Кх8** вытяжка<br>пом. 5 | | | После 1 и 2 и после получения срока у поставщика (вопроса о сроках нет); дата заказа — когда срок известен, не позднее чем за срок до начала Р-15. | срок поставки не задан (записи реестра нет) | Р-15 «кухня и мебель»: паспорта и монтажные схемы — до изготовления модулей кухни: нишу и вентзазоры задаёт модель, а не типовая схема 60 см | |
| З-4 | Стиральная машина: Пм1 (вертикальная загрузка 400 × 600 мм — условие закупки)<br>пом. 7 | | | После 1 и 2 и после получения срока у поставщика (вопроса о сроках нет); дата заказа — когда срок известен, не позднее чем за срок до начала Р-4. | срок поставки не задан (записи реестра нет) | Р-4 «черновая сантехника»: габарит и подводка — до закрытия люка и разводки | |
| З-5 | Сантехнические приборы и инсталляции: Сн1, Сн2, Сн3, См1, См2, См3<br>пом. 6, 11 | О-7: обмер: Ванная мастер (пом. 11): Ст К1-3, Ст В1-3*, Ст Т3-3*; наличие стояка ГВС, арматуры и счётчиков — по всей квартире (К-6)<br>О-2: обмер: Кабинет-библиотека (пом. 1), Гостиная-столовая (пом. 3), Кухня (пом. 5), Спальня 2 (пом. 8), Спальня мастер (пом. 10); у окон | | После 1 и 2 и после получения срока у поставщика (вопроса о сроках нет); дата заказа — когда срок известен, не позднее чем за срок до начала Р-4. | срок поставки не задан (записи реестра нет) | Р-4 «черновая сантехника»: инсталляцию ставят до обшивки ГКЛВ и до гидроизоляции стены | К-6 |
| З-6 | Керамогранит и плитка: 2 поз. по артикулу и формату, 51,07 м² по раскладке<br>пом. 4, 6, 11 | О-8: обмер: Кабинет-библиотека (пом. 1), Кладовая (пом. 2), Гостиная-столовая (пом. 3), Прихожая-холл (пом. 4), Кухня (пом. 5), Ванная (пом. 6), Постирочная (пом. 7), Спальня 2 (пом. 8), Коридор (пом. 9), Спальня мастер (пом. 10), Ванная мастер (пом. 11)<br>О-9: обмер: Кабинет-библиотека (пом. 1), Кладовая (пом. 2), Гостиная-столовая (пом. 3), Прихожая-холл (пом. 4), Кухня (пом. 5), Ванная (пом. 6), Постирочная (пом. 7), Спальня 2 (пом. 8), Коридор (пом. 9), Спальня мастер (пом. 10), Ванная мастер (пом. 11) | | После 1 и 2 и после получения срока у поставщика (вопроса о сроках нет); дата заказа — когда срок известен, не позднее чем за срок до начала Р-9. | срок поставки не задан (записи реестра нет) | Р-9 «плитка»: калибр партии измеряют до раскладки, раскладку пересчитывают до заказа | |

**Допущения и предложения на листе**

Основа листа: размеры сняты со скана обмерного плана KV оформление (см): часть подписей не читается, помещения выровнены по читаемым размерам; контрольный обмер не выполнен (К-1); высота потолка 2650 мм принята по отметкам обмера (Н = 2,50…2,66 м, ригель 2,28 м) — уточнить при обмере (К-2); толщины стен 300 / 120 мм приняты, межквартирная стена и колонны — по скану, не замерены (К-1); разрешённая мощность 15 кВт принята по типовым ТУ; при объединении двух квартир — переоформление ТУ (К-4); подрайон климата не задан — принят не северный (жилые от 2,5 м) (К-8).
Знак «*» — принято, не замерено и не подтверждено (замерить на объекте): К-6: Ст В1-3, Ст Т3-3 — положение снято со скана обмера, отдельно не замерялось; ось внутри габарита поддона См1 — обмер угла по К-6.
Знак «**» — предложение проектировщика, заказчиком не утверждено (согласовать с заказчиком): Кх8 — над индукционной панелью Кх4 нужна вытяжка: в составе кухни её не было, розетка вытяжки образца висела без потребителя.
См. лист открытых вопросов (лист 6, записи К-1, К-2, К-4, К-6, К-8).

| Изм. | Кол.уч | Лист | № док. | Подп. | Дата |
|---|---|---|---|---|---|
| Разраб. | | Кырлан А.С. | | | 04.11.26 |
| Пров. | | | | | |
| ГИП | | | | | |
| | | | | | |
| Н. контр. | | | | | |
| Утв. | | | | | |

**ГД-2026-009-АИ**

Квартира 103 м²

Общая площадь 100,72* м² · * размеры со скана, не замерены (реестр — л. 6, 7, К-1)

| Дизайн-проект интерьера | Стадия | Лист | Листов |
|---|---|---|---|
| | РП | 11 | 120 |

**График закупок и работ. Лист 1 из 3**

М б/м

**Кырлан Александр Сергеевич**

выпуск 04.11.2026 № 35b47f1c2a · стр. 11 из 130

# График закупок и работ. Лист 2 из 3

**ПРЕДВАРИТЕЛЬНО · не для производства работ · открыто пунктов: 8 (реестр — л. 6, 7)**

Что заказывать и когда не раньше чего: относительный порядок без дат; срок поставки — из данных или «не задан» с записью реестра

### Закупки: что заказывается, от чего зависит заказ и какую работу блокирует (продолжение)

| № | Позиция и где | 1. Замер до заказа | 2. Решение, выбор изделия, паспорт | 3. Условие заказа | 4. Срок поставки | 5. Блокирует работу | Закрывает вопросы реестра |
|---|---|---|---|---|---|---|---|
| З-7 | Покрытие пола (доска) и плинтус: пом. 1, 2, 3, 5, 7, 8, 9, 10<br>пом. 1, 2, 3, 5, 7, 8, 9, 10 | О-8: обмер: Кабинет-библиотека (пом. 1), Кладовая (пом. 2), Гостиная-столовая (пом. 3), Прихожая-холл (пом. 4), Кухня (пом. 5), Ванная (пом. 6), Постирочная (пом. 7), Спальня 2 (пом. 8), Коридор (пом. 9), Спальня мастер (пом. 10), Ванная мастер (пом. 11) | | После 1 и 2 и после получения срока у поставщика (вопроса о сроках нет); дата заказа — когда срок известен, не позднее чем за срок до начала Р-12. | срок поставки не задан (записи реестра нет) | Р-12 «чистовые полы»: артикул и партия — до заказа; доску привозят к чистовым полам | |
| З-8 | Встроенная мебель по замеру цеха: П1, С2, М4<br>пом. 4, 8, 10 | О-3: обмер: все помещения (К-1); до заказа мебели и дверей | | После 1 и 2 и после получения срока у поставщика (вопроса о сроках нет); дата заказа — когда срок известен, не позднее чем за срок до начала Р-15. | срок поставки не задан (записи реестра нет)<br>Ориентир практики (не срок поставщика): 4–8 нед. от замера | Р-15 «кухня и мебель»: цех замеряет по готовым стенам; производство 4–8 недель идёт параллельно с отделкой | К-1 |

### Работы: порядок и что не даёт начать

| № | Работа (стадия технологической последовательности) | После | Что должно быть к началу: условия и закупки | Не начинать, пока открыто в реестре |
|---|---|---|---|---|
| Р-1 | Демонтаж покрытий, отделки стен и потолков, дверных блоков и приборов; конструкции, стены и перегородки не трогать до технического заключения (стадия 1) | | до начала: запрошены документы на дом и БТИ; контрольный обмер до демонтажа (что видно) сделан | |
| Р-2 | Контрольный обмер на голых стенах и обследование (задание — лист «Задание на контрольный обмер») (стадия 2) | Р-1 | после снятия отделки: видны стояки, каналы, щиток, толщины стен; до заказа всего, что делают по размеру | |
| Р-3 | Черновая электрика: штробы, короба, гофра, подрозетники, щит (стадия 4) | Р-2 | до начала: план электрики с высотами утверждён; штробы в стенах — только после технического заключения; мебель расставлена | К-4: Разрешённая мощность объединённой квартиры по ТУ неизвестна, принята 15 кВт; при объединении двух квартир ТУ переоформляются. |
| Р-4 | Черновая сантехника и вентиляция: разводка, выводы, инсталляции, короба стояков (стадия 5) | Р-2 | до начала: положение стояков замерено; модели инсталляций и машины выбраны (габариты рамы, подводка); инсталляцию ставят до обшивки ГКЛВ и до гидроизоляции<br>Закупки к началу: З-4 (стиральная машина), З-5 (сантехника) | К-6: Ванная мастер (пом. |
| Р-5 | Коробки скрытых дверей, затем штукатурка стен и откосов (стадия 6) | Р-2, Р-3, Р-4 | до начала: электрика и сантехника смонтированы, штробы заделаны; коробки скрытых дверей установлены до штукатурки (поэтому заказ дверей — раньше работы)<br>Закупки к началу: З-1 (двери скрытого монтажа) | К-1: Размеры сняты со скана обмерного плана KV оформление (в см): часть подписей не читается, помещения выровнены по читаемым размерам. |
| Р-6 | Стяжка пола и тёплый пол (стадия 7) | Р-5 | до начала: штукатурка сделана; трубы под стяжкой приняты; нивелировка плиты выполнена | |
| Р-7 | Гидроизоляция санузлов и тест проливом (стадия 8) | Р-6 | до начала: стяжка набрала прочность и сухая по инструкции гидроизоляции; выводы стоят на проектных отметках | |
| Р-8 | ГКЛ: короба инсталляции и стояков, ниши, потолки (стадия 9) | Р-3, Р-4 | до начала: черновые сети в зоне коробов приняты; закладные под тяжёлое и карнизы стоят; светильники выбраны (вырезы) | |
| Р-9 | Плитка и керамогранит: стены, затем пол; фартук (стадия 10) | Р-6, Р-7, Р-8 | до начала: гидроизоляция принята; плитка выбрана, калибр партии измерен, раскладка пересчитана и подписана<br>Закупки к началу: З-6 (плитка) | |
| Р-10 | Шпаклёвка стен и потолков под окраску (стадия 11) | Р-5, Р-8, Р-9 | до начала: плитка готова (грязные работы закончены); штукатурка и ГКЛ сухие | |

**Допущения и предложения на листе**

Основа листа: размеры сняты со скана обмерного плана KV оформление (см): часть подписей не читается, помещения выровнены по читаемым размерам; контрольный обмер не выполнен (К-1); высота потолка 2650 мм принята по отметкам обмера (Н = 2,50…2,66 м, ригель 2,28 м) — уточнить при обмере (К-2); толщины стен 300 / 120 мм приняты, межквартирная стена и колонны — по скану, не замерены (К-1); разрешённая мощность 15 кВт принята по типовым ТУ; при объединении двух квартир — переоформление ТУ (К-4); подрайон климата не задан — принят не северный (жилые от 2,5 м) (К-8).

См. лист открытых вопросов (лист 6, записи К-1, К-2, К-4, К-8).

| Изм. | Кол.уч | Лист | № док. | Подп. | Дата |
|---|---|---|---|---|---|
| Разраб. | | Кырлан А.С. | | | 04.11.26 |
| Пров. | | | | | |
| ГИП | | | | | |
| | | | | | |
| Н. контр. | | | | | |
| Утв. | | | | | |

**ГД-2026-009-АИ**

Квартира 103 м²

Общая площадь 100,72* м² · * размеры со скана, не замерены (реестр — л. 6, 7, К-1)

Дизайн-проект интерьера

| Стадия | Лист | Листов |
|---|---|---|
| РП | 12 | 120 |

**График закупок и работ. Лист 2 из 3**

М б/м

**Кырлан Александр Сергеевич**

выпуск 04.11.2026 № 35b47f1c2a · стр. 12 из 130

# График закупок и работ. Лист 3 из 3

**ПРЕДВАРИТЕЛЬНО · не для производства работ · открыто пунктов: 8 (реестр — л. 6, 7)**

Что заказывать и когда не раньше чего: относительный порядок без дат; срок поставки — из данных или «не задан» с записью реестра

## Работы: порядок и что не даёт начать (продолжение)

| № | Работа (стадия технологической последовательности) | После | Что должно быть к началу: условия и закупки | Не начинать, пока открыто в реестре |
|---|---|---|---|---|
| Р-11 | Окраска стен, потолков, откосов (стадия 13) | Р-10 | до начала: шпаклёвка отшлифована и огрунтована; выкрасы утверждены, колеровка одной партией | |
| Р-12 | Чистовые полы: инженерная доска (стадия 14) | Р-9, Р-11 | до начала: влажность основания в норме, мокрые работы закончены; доска выбрана и привезена<br>Закупки к началу: З-7 (доска и плинтус) | |
| Р-13 | Полотна межкомнатных дверей, плинтусы, пороги (стадия 15) | Р-11, Р-12 | до начала: чистовой пол уложен; полотна скрытых дверей — после чистовой отделки стен | |
| Р-14 | Чистовая электрика и сантехника: механизмы, светильники, смесители, приборы (стадия 16) | Р-11, Р-13 | до начала: отделка готова; механизмы, светильники и приборы выбраны и привезены | |
| Р-15 | Кухня, встроенная и корпусная мебель, бытовая техника (стадия 17) | Р-13, Р-14 | до начала: чистовая сантехника и электрика подведены к местам мебели; замер кухни снят по готовым стенам (после штукатурки или плитки, до чистового пола)<br>Закупки к началу: З-2 (кухонный гарнитур), З-3 (техника кухни), З-8 (мебель по замеру) | К-1: Размеры сняты со скана обмерного плана KV оформление (в см): часть подписей не читается, помещения выровнены по читаемым размерам. |
| Р-16 | Сдача: осмотр по чек-листу, дефектная ведомость, устранение замечаний (стадия 18) | Р-14, Р-15 | до начала: всё смонтировано; акты скрытых работ подписаны | |

## Примечания

1. Порядок работ — стадии технологической последовательности из 16 позиций, присутствующих в этом проекте (по строкам ведомости объёмов); остальные стадии таблицы knowledge/remont-tehnologiya.md в проекте не встречаются. Длительности работ не печатаются: их нет ни в данных, ни в нормах для этого объекта.
2. Типовые сроки — ориентир практики, не срок поставщика: скрытые двери — короб около 10 дн., полотно под покраску до 3 нед., шпон 4–5 нед., в среднем около 30 дн. (knowledge/workers/foreman.md, п. 2.4 (profil-doors)); кухня и корпусная мебель — 4–8 недель от замера (knowledge/remont-tehnologiya.md, разд. 2; knowledge/workers/foreman.md, п. 2.4). Заказ по ориентиру не назначается: срок получают у поставщика (вопрос реестра), после чего заказ планируют «не позднее чем за срок до начала работы».
3. Условия заказа берутся из реестра открытых вопросов и задания на контрольный обмер: позиция заказывается, когда закрыты замер (графа 1) и решение (графа 2). Закрывать их может только факт или решение автора с подписью; снять строку с листа можно только закрыв запись реестра.
4. Заказ по размеру до контрольного обмера не делают: двери, кухня и встроенная мебель зависят от обмера (К-11, К-13); скрытые двери, кроме того, зависят от решения по нише санузла 2 (проём Д-5 в перегородке П-1).
5. Номера листов — по ведомости рабочих чертежей комплекта (лист «Общие данные»).

**Допущения и предложения на листе**

Основа листа: размеры сняты со скана обмерного плана KV оформление (см): часть подписей не читается, помещения выровнены по читаемым размерам; контрольный обмер не выполнен (К-1); высота потолка 2650 мм принята по отметкам обмера (Н = 2,50…2,66 м, ригель 2,28 м) — уточнить при обмере (К-2); толщины стен 300 / 120 мм приняты, межквартирная стена и колонны — по скану, не замерены (К-1); разрешённая мощность 15 кВт принята по типовым ТУ; при объединении двух квартир — переоформление ТУ (К-4); подрайон климата не задан — принят не северный (жилые от 2,5 м) (К-8).
См. лист открытых вопросов (лист 6, записи К-1, К-2, К-4, К-8).

| Изм. | Кол.уч | Лист | № док. | Подп. | Дата |
|---|---|---|---|---|---|
| Разраб. | | Кырлан А.С. | | | 04.11.26 |
| Пров. | | | | | |
| ГИП | | | | | |
| | | | | | |
| Н. контр. | | | | | |
| Утв. | | | | | |

**ГД-2026-009-АИ**

Квартира 103 м²

Общая площадь 100,72* м² · * размеры со скана, не замерены (реестр — л. 6, 7, К-1)

Дизайн-проект интерьера

| Стадия | Лист | Листов |
|---|---|---|
| РП | 13 | 120 |

**График закупок и работ. Лист 3 из 3**

М б/м

**Кырлан Александр Сергеевич**

выпуск 04.11.2026 № 35b47f1c2a · стр. 13 из 130

01

# Архитектурные решения




Кырлан Александр Сергеевич

выпуск 04.11.2026 · 35b47f1c2a · стр. 14 из 130

# Обмерный план

Существующее положение · размеры в мм · отметки от чистого пола

**ПРЕДВАРИТЕЛЬНО · не для производства работ · открыто пунктов: 8 (реестр — л. 6, 7)**

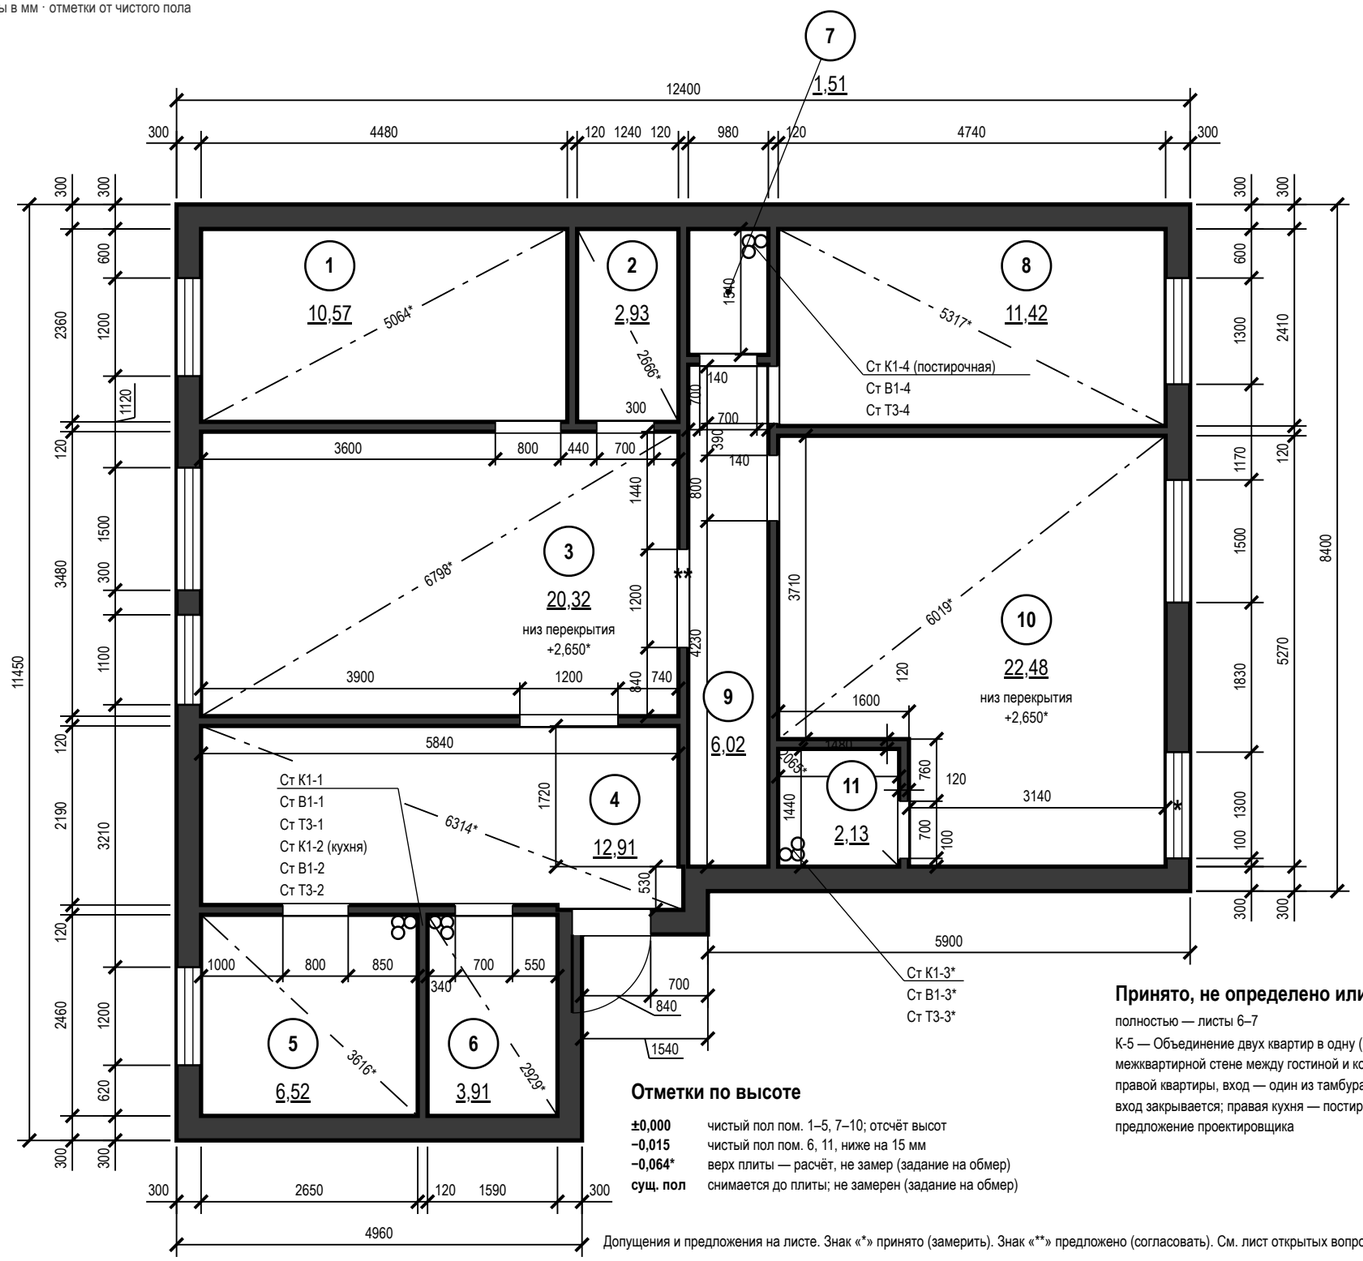


## Экспликация помещений

| № | Наименование | Площадь, м² |
|---|---|---|
| 1 | Кабинет-библиотека | 10,57 |
| 2 | Кладовая | 2,93 |
| 3 | Гостиная-столовая | 20,32 |
| 4 | Прихожая-холл | 12,91 |
| 5 | Кухня | 6,52 |
| 6 | Ванная | 3,91 |
| 7 | Постирочная | 1,51 |
| 8 | Спальня 2 | 11,42 |
| 9 | Коридор | 6,02 |
| 10 | Спальня мастер | 22,48 |
| 11 | Ванная мастер | 2,13 |
| | **Итого (общая площадь)** | **100,72** |

## Условные обозначения

- существующие стены (сечение)
- окно (рама, остекление)
- проём существующий, без заполнения (откосы)
- стояк: К1 — канализация, В1 — ХВС, Т3 — ГВС
- ** — «**» — предложение проектировщика, заказчиком не утверждено
- диагональ помещения — контроль прямоугольности
- (1) — номер помещения, площадь м²
- * — «*» — принято, не замерено и не подтверждено

## Отметки по высоте

| | |
|---|---|
| **±0,000** | чистый пол пом. 1–5, 7–10; отсчёт высот |
| **−0,015** | чистый пол пом. 6, 11, ниже на 15 мм |
| **−0,064*** | верх плиты — расчёт, не замер (задание на обмер) |
| **сущ. пол** | снимается до плиты; не замерен (задание на обмер) |

## Принято, не определено или спорно

полностью — листы 6–7

К-5 — Объединение двух квартир в одну (проём в межквартирной стене между гостиной и коридором правой квартиры, вход — один из тамбура, второй вход закрывается; правая кухня — постирочная) предложение проектировщика

Допущения и предложения на листе. Знак «*» принято (замерить). Знак «**» предложено (согласовать). См. лист открытых вопросов (лист 6).

## Примечания

1. Размеры — в мм по чистым поверхностям стен до отделки (по плану заказчика); площади — в м² по тем же размерам. До начала работ выполнить контрольный обмер.
2. Источник плана — допущение, не замер: растровый скан плана заказчика, размеры сняты с размерных цепочек, на объекте не замерены. Реестр: листы 6–7, вопросы К-1, К-6.
3. Знак «*» у проёма — положение не замерено; реестр: листы 6–7, вопрос К-1.
4. Знак «*» у стояка — положение принято, не замерено (Ст К1-3*, Ст В1-3*, Ст Т3-3*); сверить на объекте до разметки. Реестр: листы 6–7, вопрос К-6.
5. За отметку ±0,000 принят чистый пол, не существующий (блок отметок). «Низ перекрытия» у марки помещения — отметка низа перекрытия от ±0,000, как на развёртках и плане потолков (не высота потолка: потолок — по плану потолков); отметка со знаком «*» — принятая, не замер (вопрос К-2).
6. Толщины стен: наружные 300 мм, перегородки 120 мм; отличающиеся толщины и уступы — размерами на плане.
7. Несущие стены не определены: до технического заключения все стены считать несущими; проёмы и штробы в них не выполнять.
8. Дверные проёмы показаны без заполнения (двери — лист 17); высота дверных проёмов 2100 мм, проёмов без двери 2100 мм; низ окон (подоконник) 720, 735, 763, 783, 825 мм от чистого пола, высота окон 1560, 1550, 1552, 1548 мм.
9. Диагонали — контрольные размеры; «*» — расчёт по принятому контуру (К-1), при обмере заменить замеренным; расхождение более 5 мм подписать на плане как перекос.
10. Размеры проверить на месте до начала работ; расхождение контрольных промеров ≤ 2 %.
11. Размеры короче 1 мм на листе цепочкой не показаны (две выносные линии на таком расстоянии сливаются): пом. 9, стена Б — 20 мм от угла до проёма.

1000 мм · печать 1:1

| Изм. | Кол.уч | Лист | № док. | Подп. | Дата |
|---|---|---|---|---|---|
| Разраб. | | Кырлан А.С. | | | 04.11.26 |
| Пров. | | | | | |
| ГИП | | | | | |
| Н. контр. | | | | | |
| Утв. | | | | | |

**ГД-2026-009-АИ**

Квартира 103 м²

Общая площадь 100,72* м² · * размеры со скана, не замерены (реестр — л. 6, 7, К-1)

Дизайн-проект интерьера

| Стадия | Лист | Листов |
|---|---|---|
| РП | 14 | 120 |

**Обмерный план**

М 1:75


**Кырлан Александр Сергеевич**

выпуск 04.11.2026 № 35b47f1c2a · стр. 15 из 130

# План демонтажа и монтажа перегородок

Перепланировка не выполняется · существующие стены сохраняются · размеры в мм

**ПРЕДВАРИТЕЛЬНО · не для производства работ · открыто пунктов: 8 (реестр — л. 6, 7)**

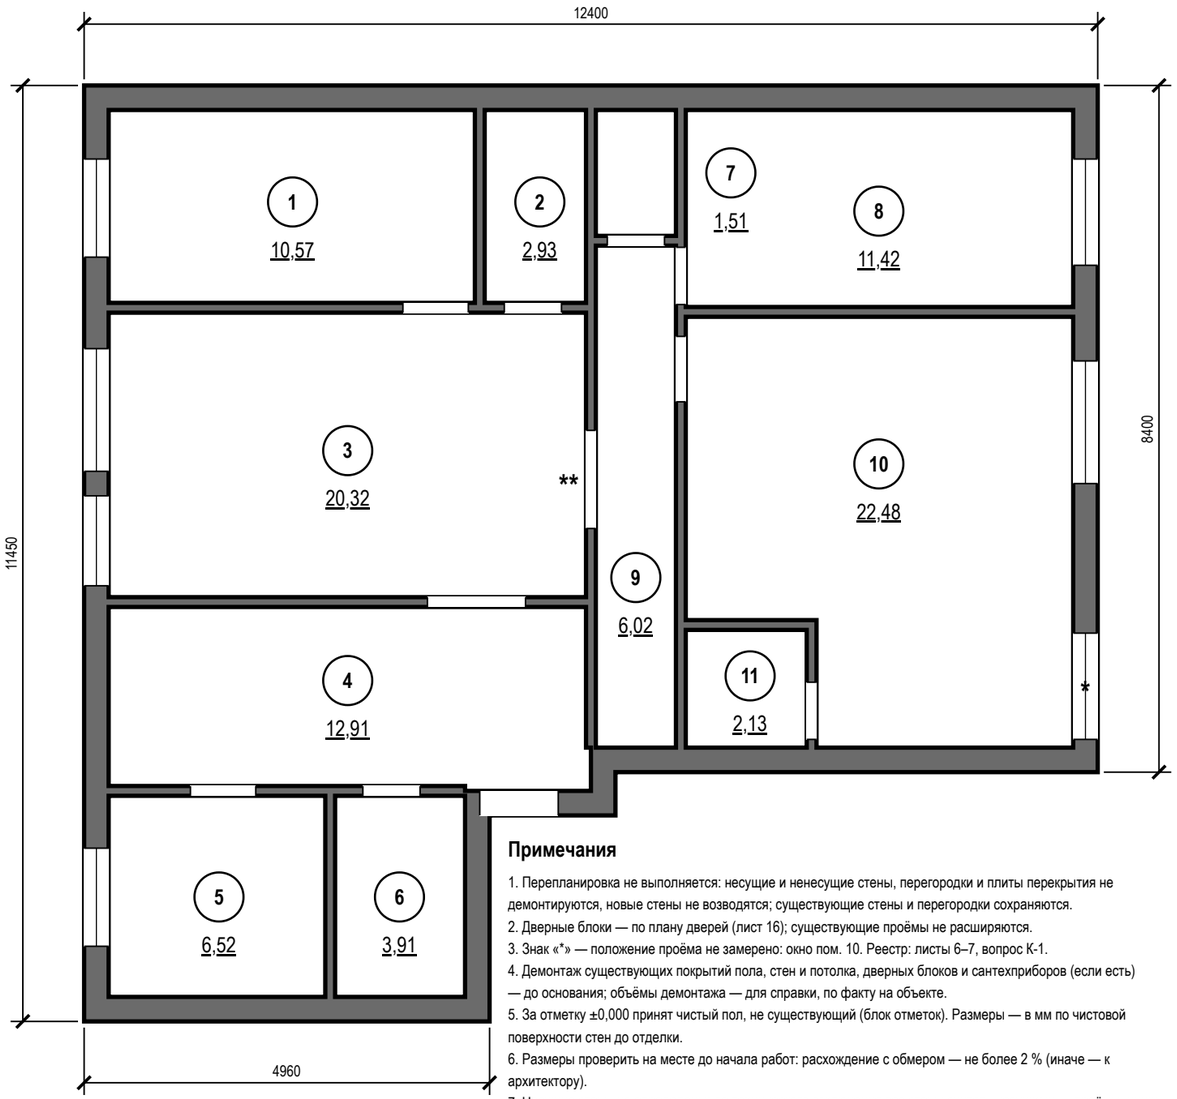


## Условные обозначения

- существующие стены — сохраняются; несущие не определены — считать несущими
- демонтируемые конструкции — на плане нет
- возводимые перегородки — на плане нет
- проём существующий, без заполнения (откосы)
- (1) номер помещения, площадь м²
- * — «*» — принято, не замерено и не подтверждено

## Отметки по высоте

| | | | |
|---|---|---|---|
| **±0,000** | чистый пол пом. 1–5, 7–10; отсчёт высот | **−0,064*** | верх плиты — расчёт, не замер (задание на обмер) |
| **−0,015** | чистый пол пом. 6, 11, ниже на 15 мм | **сущ. пол** | снимается до плиты; не замерен (задание на обмер) |

## Примечания

1. Перепланировка не выполняется: несущие и ненесущие стены, перегородки и плиты перекрытия не демонтируются, новые стены не возводятся; существующие стены и перегородки сохраняются.
2. Дверные блоки — по плану дверей (лист 16); существующие проёмы не расширяются.
3. Знак «*» — положение проёма не замерено: окно пом. 10. Реестр: листы 6–7, вопрос К-1.
4. Демонтаж существующих покрытий пола, стен и потолка, дверных блоков и сантехприборов (если есть) — до основания; объёмы демонтажа — для справки, по факту на объекте.
5. За отметку ±0,000 принят чистый пол, не существующий (блок отметок). Размеры — в мм по чистовой поверхности стен до отделки.
6. Размеры проверить на месте до начала работ: расхождение с обмером — не более 2 % (иначе — к архитектору).
7. Несущие стены не определены: до технического заключения все стены считать несущими — проёмы, ниши и штробы в них не выполнять.

**Допущения и предложения на листе**

Основа листа: размеры сняты со скана обмерного плана KV оформление (см): часть подписей не читается, помещения выровнены по читаемым размерам; контрольный обмер не выполнен (К-1); высота потолка 2650 мм принята по отметкам обмера (Н = 2,50…2,66 м, ригель 2,28 м) — уточнить при обмере (К-2); толщины стен 300 / 120 мм приняты, межквартирная стена и колонны — по скану, не замерены (К-1); разрешённая мощность 15 кВт принята по типовым ТУ; при объединении двух квартир — переоформление ТУ (К-4); подрайон климата не задан — принят не северный (жилые от 2,5 м) (К-8).

Знак «*» — принято, не замерено и не подтверждено (замерить на объекте): К-1: окно пом. 10 (стена Б) — Окно 1300 при смещение 3500 на стене Б основной части (длина 3830) выходило за стену на 970 мм.

Знак «**» — предложение проектировщика, заказчиком не утверждено (согласовать с заказчиком): К-5: дверь пом. 3 (стена Б) — проём в межквартирной стене — объединение квартир, предложение до техзаключения.

См. лист открытых вопросов (лист 6, записи К-1, К-2, К-4, К-5, К-8).

1000 мм · печать 1:1

| Изм. | Кол.уч | Лист | № док. | Подп. | Дата |
|---|---|---|---|---|---|
| Разраб. | | Кырлан А.С. | | | 04.11.26 |
| Пров. | | | | | |
| ГИП | | | | | |
| | | | | | |
| Н. контр. | | | | | |
| Утв. | | | | | |

**ГД-2026-009-АИ**

Квартира 103 м²

Общая площадь 100,72* м² · * размеры со скана, не замерены (реестр — л. 6, 7, К-1)

Дизайн-проект интерьера

| Стадия | Лист | Листов |
|---|---|---|
| РП | 15 | 120 |

**План демонтажа и монтажа перегородок**


М 1:75

**Кырлан Александр Сергеевич**

# План дверей

Проёмы, марки заполнения, привязки · размеры в мм



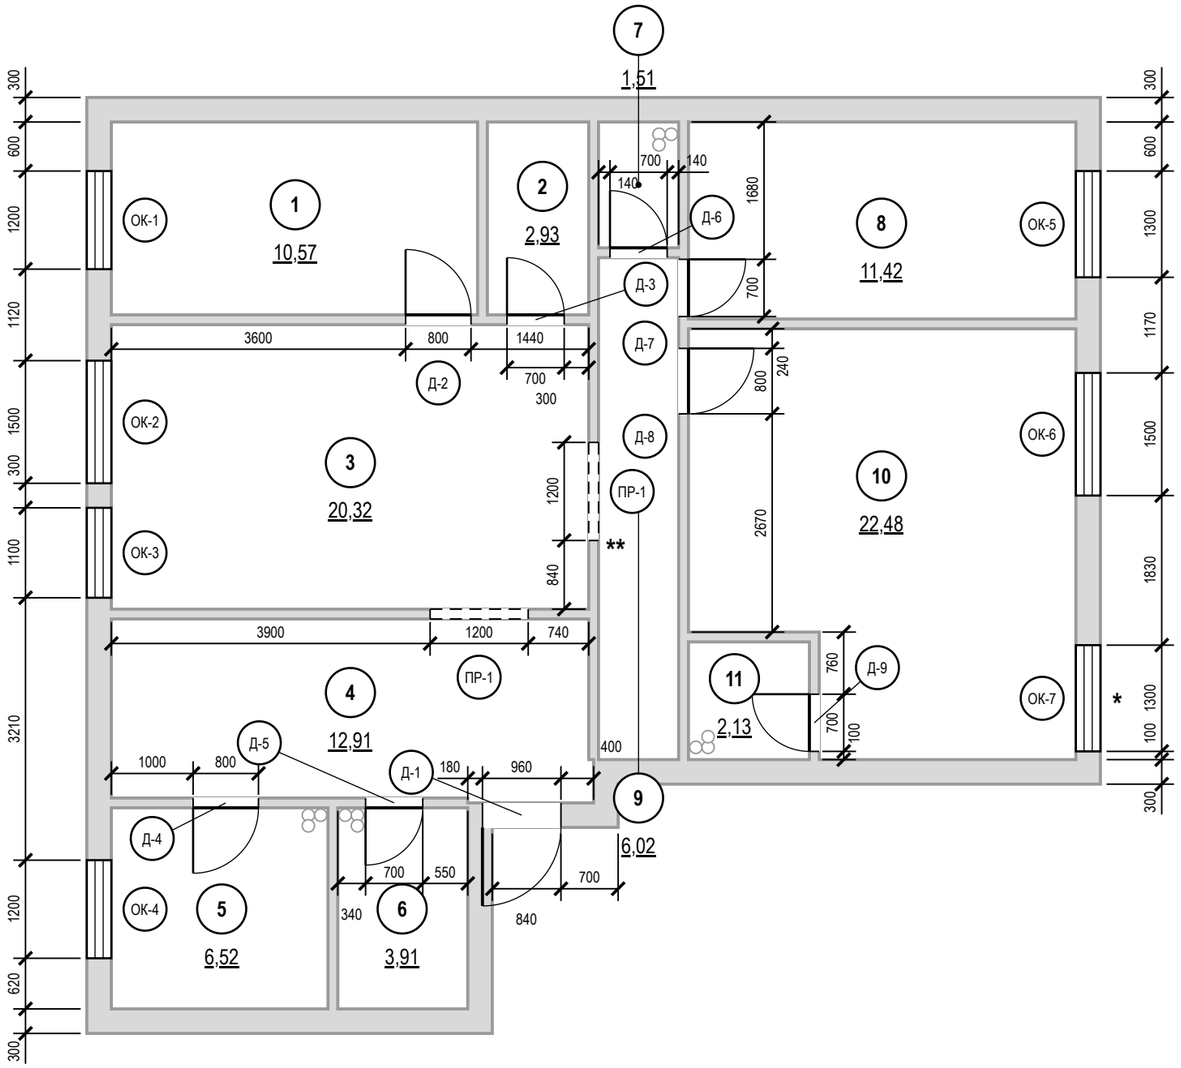


## Условные обозначения

- стены (подложка обмера)
- дверь распашная, дуга открывания
- дверь скрытого монтажа
- дверь входная (полотно толще)
- портал (штрих — перемычка)
- оконный блок
- Д — марка типа (Д-N, ПР-N, ОК-N)
- 1 — номер помещения, площадь м²
- * — «*» — принято, не замерено и не подтверждено
- ** — «**» — предложение проектировщика, заказчиком не утверждено

## Примечания

1. Размеры проёмов и привязки — в миллиметрах от чистых граней стен до отделки; привязка — от угла того помещения, со стороны которого стоит размер. Размер проёма — ширина × высота от чистого пола 0,000. Размеры на плане — проёмов, не полотен: полотно — в ведомости, коробка — по системе. Откос от угла помещения до проёма с коробкой — не менее 50 мм.
2. Марки в кружках — типы заполнения проёмов (ГОСТ 21.501-2018, п. 5.3.2); одна марка — один типоразмер; количество сверено с планом.
3. Д-2…Д-9 — существующие проёмы, до техзаключения не расширять.
4. Д-1: дуга наружу — по плану заказчика, не проверено; блок оставить или заменить — не решено.
5. Размеры проёмов и привязки сняты со скана плана заказчика и на объекте не замерены (обмерный план — лист 14).
6. Знак «*» у проёма — допущение: положение проёма не замерено (окно пом. 10, стена Б); размер напечатан как принятый; в ведомости — знак «*» в графе «Прим.». Реестр: листы 6–7, вопрос К-1.
7. Экспликация помещений — лист 14; в марках помещений — номер и площадь, м².
8. Ведомость заполнения проёмов, открывание полотен, заказ и порядок монтажа блоков — лист 17.
9. Привязка проёма к углу помещения меньше 1 мм на листе, размер на плане не показан: Д-7 — 30 мм.

**Допущения и предложения на листе**

Основа листа: размеры сняты со скана обмерного плана KV оформление (см): часть подписей не читается, помещения выровнены по читаемым размерам; контрольный обмер не выполнен (К-1); высота потолка 2650 мм принята по отметкам обмера (Н = 2,50…2,66 м, ригель 2,28 м) — уточнить при обмере (К-2); толщины стен 300 / 120 мм приняты, межквартирная стена и колонны — по скану, не замерены (К-1); разрешённая мощность 15 кВт принята по типовым ТУ; при объединении двух квартир — переоформление ТУ (К-4); подрайон климата не задан — принят не северный (жилые от 2,5 м) (К-8).

Знак «*» — принято, не замерено и не подтверждено (замерить на объекте): К-1: окно пом. 10 (стена Б) — Окно 1300 при смещение 3500 на стене Б основной части (длина 3830) выходило за стену на 970 мм; К-6: Ст К1-3, Ст В1-3, Ст Т3-3 — положение снято со скана обмера, отдельно не замерялось; ось внутри габарита поддона См1 — обмер угла по К-6.

Знак «**» — предложение проектировщика, заказчиком не утверждено (согласовать с заказчиком): К-5: дверь пом. 3 (стена Б) — проём в межквартирной стене — объединение квартир, предложение до техзаключения.

Изменения по листу без подписи: ИЗ-1.

См. лист открытых вопросов (лист 6, записи ИЗ-1, К-1, К-2, К-4–К-6, К-8).

1000 мм · печать 1:1

| Изм. | Кол.уч | Лист | № док. | Подп. | Дата |
|---|---|---|---|---|---|
| Разраб. | | Кырлан А.С. | | | 04.11.26 |
| Пров. | | | | | |
| ГИП | | | | | |
| Н. контр. | | | | | |
| Утв. | | | | | |

**ГД-2026-009-АИ**

Квартира 103 м²

Общая площадь 100,72* м² · * размеры со скана, не замерены (реестр — л. 6, 7, К-1)

Дизайн-проект интерьера

| Стадия | Лист | Листов |
|---|---|---|
| РП | 16 | 120 |

**План дверей**

М 1:75

Кырлан Александр Сергеевич


# Ведомость заполнения проёмов

Проёмы, полотна, отделка, фурнитура · размеры в мм

## Ведомость заполнения проёмов

| Марка | Наименование, обозначение | Проём ш×в, мм | Полотно (расч.) | Кол. | Откр. | Отделка полотна | Фурнитура | Прим. |
|---|---|---|---|---|---|---|---|---|
| Д-1 | Блок дверной входной, ГОСТ 31173-2016 | 960×2100 | блок задать | 1 | Л | в комплекте блока | в комплекте блока (замки, глазок) | наружу |
| Д-2 | Дверь скрытого монтажа, UNION FILO-60 Piatto | 800×2100 | 700×2000 | 1 | П | окраска No. 291 с двух сторон | скрытые петли 3D, магнитный замок | |
| Д-3 | Дверь скрытого монтажа, UNION FILO-60 Piatto | 700×2100 | 600×2000 | 1 | П | S 0502-Y — пом. 2, No. 291 — пом. 3 | скрытые петли 3D, магнитный замок | |
| Д-4 | Дверь скрытого монтажа, UNION FILO-60 Piatto | 800×2100 | 700×2000 | 1 | Л | окраска No. 291 с двух сторон | скрытые петли 3D, магнитный замок | |
| Д-5 | Дверь скрытого монтажа, UNION FILO-60 Piatto | 700×2100 | 600×2000 | 1 | Л | в тон облицовки — пом. 6, No. 291 — пом. 4 | скрытые петли 3D, магнитный замок, фиксатор WC | порог 15 |
| Д-6 | Дверь скрытого монтажа, UNION FILO-60 Piatto | 700×2100 | 600×2000 | 1 | П | S 0502-Y — пом. 7, No. 291 — пом. 9 | скрытые петли 3D, магнитный замок | |
| Д-7 | Дверь скрытого монтажа, UNION FILO-60 Piatto | 700×2100 | 600×2000 | 1 | П | окраска No. 291 с двух сторон | скрытые петли 3D, магнитный замок | |
| Д-8 | Дверь скрытого монтажа, UNION FILO-60 Piatto | 800×2100 | 700×2000 | 1 | П | окраска No. 291 с двух сторон | скрытые петли 3D, магнитный замок | |
| Д-9 | Дверь скрытого монтажа, UNION FILO-60 Piatto | 700×2100 | 600×2000 | 1 | Л | в тон облицовки — пом. 11, No. 291 — пом. 10 | скрытые петли 3D, магнитный замок, фиксатор WC | порог 15 |
| ПР-1 | Портал без заполнения | 1200×2100 | | 2 | | | | ** пом. 3; б/п |
| ОК-1 | Блок оконный, ГОСТ 23166-2021; стекло — триплекс | 1200×1560 | | 1 | | | | низ 720 |
| ОК-2 | Блок оконный, ГОСТ 23166-2021; стекло — триплекс | 1500×1550 | | 1 | | | | низ 735 |
| ОК-3 | Блок оконный, ГОСТ 23166-2021; стекло — триплекс | 1100×1550 | | 1 | | | | низ 735 |
| ОК-4 | Блок оконный, ГОСТ 23166-2021; стекло — триплекс | 1200×1550 | | 1 | | | | низ 763 |
| ОК-5 | Блок оконный, ГОСТ 23166-2021; стекло — триплекс | 1300×1552 | | 1 | | | | низ 783 |
| ОК-6 | Блок оконный, ГОСТ 23166-2021; стекло — триплекс | 1500×1548 | | 1 | | | | низ 825 |
| ОК-7 | Блок оконный, ГОСТ 23166-2021; стекло — триплекс | 1300×1548 | | 1 | | | | * пом. 10; низ 825 |

**Схемы дверных блоков (1:75) — вид со стороны открывания; вершина треугольника — сторона петель**

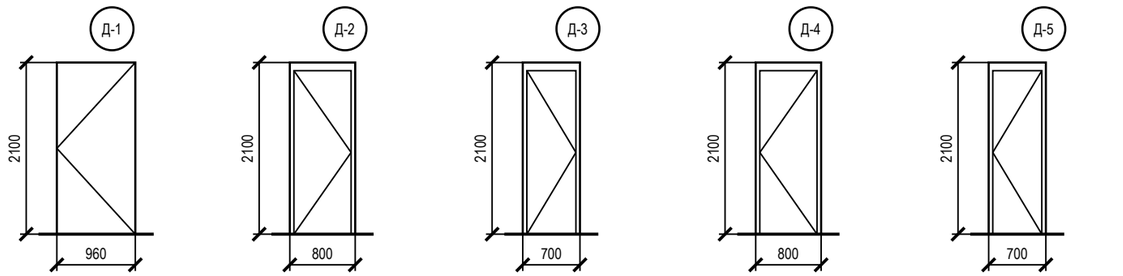


**Допущения и предложения на листе**

Основа листа: размеры сняты со скана обмерного плана KV оформление (см): часть подписей не читается, помещения выровнены по читаемым размерам; контрольный обмер не выполнен (К-1); высота потолка 2650 мм принята по отметкам обмера (Н = 2,50…2,66 м, ригель 2,28 м) — уточнить при обмере (К-2); толщины стен 300 / 120 мм приняты, межквартирная стена и колонны — по скану, не замерены (К-1); разрешённая мощность 15 кВт принята по типовым ТУ; при объединении двух квартир — переоформление ТУ (К-4); подрайон климата не задан — принят не северный (жилые от 2,5 м) (К-8).

См. лист открытых вопросов (лист 6, записи К-1, К-2, К-4, К-8).

## Примечания

1. Марки проёмов — те же, что на плане размещения дверей (лист 16); привязки проёмов — там же.
2. Открывание: Л — петли слева, П — справа, если смотреть со стороны, куда открывается полотно (на себя).
3. Остекление окон: ОК-1 (пом. 1) — триплекс; ОК-2 (пом. 3) — триплекс; ОК-3 (пом. 3) — триплекс; ОК-4 (пом. 5) — триплекс; ОК-5 (пом. 8) — триплекс; ОК-6 (пом. 10) — триплекс; ОК-7 (пом. 10) — триплекс. Тип стекла указать при заказе оконных блоков; замена на другое стекло — только по согласованию с автором проекта.
4. ОК-1, ОК-2, ОК-3, ОК-4, ОК-5, ОК-6, ОК-7: низ остекления 720 и 735 и 763 и 783 и 825 мм — ниже 900 мм от чистого пола, поэтому окно заказывать с безопасным стеклом (триплекс); ограждение проёма в проекте не задано (СП 54.13330.2022, п. 6.4.9; ГОСТ Р 56926).
5. Скрытые двери (Д-2…Д-9): проём замерить в чистоте; блок заказать до штукатурки (≈ 30 дн.), короб ставить до штукатурки; полотно навесить после чистовой отделки, красить в цвет стен. Порядок — практика монтажа, изготовитель подтверждает.
6. Полотно «расч.» — по проёму и ряду изделия с запасом по каталогам, заказ — по таблице проёмов модели; Д-2…Д-9: проём 2100, а под полотно 2000 по каталогам нужен 2050–2080, под 2100 — 2150–2180: высоту проёма — по модели; Д-1: входной блок по ГОСТ 31173-2016 — задать при выборе блока.

| Изм. | Кол.уч | Лист | № док. | Подп. | Дата |
|---|---|---|---|---|---|
| Разраб. | | Кырлан А.С. | | | 04.11.26 |
| Пров. | | | | | |
| ГИП | | | | | |
| | | | | | |
| Н. контр. | | | | | |
| Утв. | | | | | |

**ГД-2026-009-АИ**

Квартира 103 м²

Общая площадь 100,72* м² · * размеры со скана, не замерены (реестр — л. 6, 7, К-1)

Дизайн-проект интерьера

| Стадия | Лист | Листов |
|---|---|---|
| РП | 17 | 120 |

**Ведомость заполнения проёмов**

М б/м

**Кырлан Александр Сергеевич**

выпуск 04.11.2026 № 35b47f1c2a · стр. 18 из 130

02

# Планировочное решение

Кырлан Александр Сергеевич

выпуск 04.11.2026 · 35b47f1c2a · стр. 19 из 130

# Концепция интерьера


Мид-сенчури · схема комплементарная · 60/30/10 · материалы, образы и зонирование

**ПРЕДВАРИТЕЛЬНО · не для производства работ · открыто пунктов: 8 (реестр — л. 6, 7)**

## Идея

Стиль — мид-сенчури: оптимизм, функциональность, тёплое дерево, лёгкость, ретро без китча, связь с улицей, графичные акценты. Модернизм середины века 65 % + ар-деко 35 %. Стены — School House White No. 291, потолки белый S 0502-Y; второй план — орех и тик, оливковый Bancha No. 298, сине-серый Inchyra Blue No. 289; акценты горчица S 2050-Y20R, терракота S 3050-Y70R, тил S 5030-B10G, изумрудный бархат S 5040-B90G; металл — латунь. Мебель — авторские модели середины века (как предложение, модели уточняются с заказчиком). Цветовая схема комплементарная, пропорция 60/30/10: база на стенах и потолках, вторичный цвет — в текстиле и мягкой мебели, акцент — точечно.

## Мудборд: материалы и фактуры

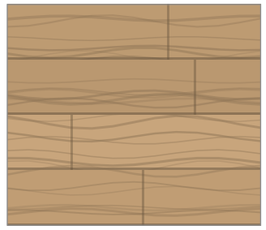

1167-4250
пол



A8UZ
пол, стены



Белый с лёгкой желтизной · NCS S 0502-Y
потолок, стены, плинтус




School House White — тёплый меловой белый · Farrow & Ball No. 291
стены, плинтус, потолок




Inchyra Blue — тёмный сине-серый · Farrow & Ball No. 289
акцент (стена А)



Tanner's Brown — тёмный шоколад · Farrow & Ball No. 255
акцент (стена А)

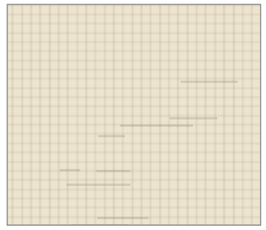

Лён, NCS S 1005-Y20R
портьеры-волна, Портьеры-волна

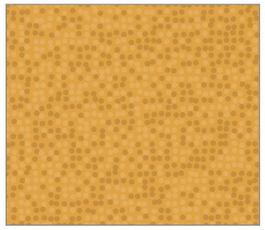

Шерсть, NCS S 2050-Y20R
ковёр под рабочей зоной, ковёр под кроватью



Бархат, Farrow & Ball No. 255
Подушки декоративные на диван

## Палитра 60/30/10




60 % база — Farrow & Ball No. 291 School House White — тёплый меловой белый, LRV 73; NCS S 0502-Y Белый с лёгкой желтизной, LRV 95

30 % вторичный — Farrow & Ball No. 298 Bancha — оливковый середины века, LRV 14; Farrow & Ball No. 289 Inchyra Blue — тёмный сине-серый, LRV 13; Farrow & Ball No. 255 Tanner's Brown — тёмный шоколад, LRV 7

10 % акцент — NCS S 2050-Y20R Горчичный, LRV 42; NCS S 3050-Y70R Терракотовый / жжёный оранжевый, LRV 18; NCS S 5030-B10G Тил, LRV 12; NCS S 5040-B90G Изумрудный, LRV 8

## Функциональное зонирование (М 1:200)




- дневная зона: гостиная, кухня, столовая
- ночная зона: спальни
- мокрая зона: санузлы
- хранение: гардеробная, кладовая
- вход и коммуникации
- функциональная зона в помещении
- (1) номер помещения (лист 19)

## Образы помещений

**3. Гостиная-столовая** — 20,32 м²
стены Farrow & Ball No. 291; акцент No. 255 на стене А

**5. Кухня** — 6,52 м²
стены Farrow & Ball No. 291
пол — 1167-4250

**8. Спальня 2** — 11,42 м²
стены Farrow & Ball No. 291; акцент No. 289 на стене А

**10. Спальня мастер** — 22,48 м²
стены Farrow & Ball No. 291; акцент No. 289 на стене А

**1. Кабинет-библиотека** — 10,57 м²
стены Farrow & Ball No. 291; акцент No. 289 на стене А

**4. Прихожая-холл** — 12,91 м²
стены Farrow & Ball No. 291
пол — A8UZ

**9. Коридор** — 6,02 м²
стены Farrow & Ball No. 291
пол — 1167-4250

**7. Постирочная** — 1,51 м²
стены NCS S 0502-Y
пол — 1167-4250

**6. Ванная** — 3,91 м²
стены Atlas Concorde A8UZ
пол — Atlas Concorde Marvel Travertine Sand

**11. Ванная мастер** — 2,13 м²
стены Atlas Concorde A8UZ
пол — Atlas Concorde Marvel Travertine Sand

**2. Кладовая** — 2,93 м²
стены NCS S 0502-Y
пол — 1167-4250

## Материалы и отделка

**1167-4250**
пол — пом. 1, 2, 3, 5, 7, 8, 9, 10

**A8UZ**
пол, стены — пом. 4, 6, 11

**Керамогранит матовый**
тон F497; 600×600
фартук — пом. 5

**Atlas Concorde Marvel Travertine Sand Cross 60×60 Matte Sensitech**
арт. AFUL (той же коллекции, что стены A8UZ; тон сверить по образцу); Atlas Concorde Marvel Travertine Sand Cross 60×60 Matte Sensitech
пол — пом. 6, 11

**Farrow & Ball No. 291 School House White — тёплый меловой белый, LRV 73**
Farrow & Ball Modern Emulsion, матовая
стены, плинтус, потолок — пом. 1, 3, 4, 5, 8, 9, 10

**NCS S 0502-Y Белый с лёгкой желтизной, LRV 95**
Tikkurila Anti-Reflex 2, глубокоматовая
потолок, стены, плинтус — пом. 1, 2, 4, 6, 7, 8, 9, 10, 11

**Farrow & Ball No. 289 Inchyra Blue — тёмный сине-серый, LRV 13**
акцентная стена
акцент (стена А) — пом. 1, 8, 10

**Farrow & Ball No. 255 Tanner's Brown — тёмный шоколад, LRV 7**
акцентная стена
акцент (стена А) — пом. 3

## Текстиль и металл

**Лён, NCS S 1005-Y20R**
портьеры-волна, Портьеры-волна

**Шерсть, NCS S 2050-Y20R**
ковёр под рабочей зоной, ковёр под кроватью

**Шерсть, Farrow & Ball No. 289**
плед на кровать

**Шерсть, Farrow & Ball No. 298**
ковёр мягкой группы, ковёр под кроватью

**Шерсть, Farrow & Ball No. 255**
Плед на диван

**Вуаль, NCS S 0502-Y**
тюль

**Букле, NCS S 3050-Y70R**
подушки декоративные на кровать

**Вуаль, Farrow & Ball No. 291**
Тюль-вуаль

**Бархат, Farrow & Ball No. 255**
Подушки декоративные на диван

**Чёрный матовый металл**
зеркало, зеркало в рост

## Чего избегаем

1) Ретро-парк: все акценты сразу (оранжевый + бирюза + горчица + атомные обои) — это тематический кафе-интерьер
2) Дешёвые реплики с неправильными пропорциями (толстые прямые ножки, утяжелённые спинки)
3) Холодный серо-белый сканди с ламинатом под беленый дуб — у мид-сенчури тёплое тёмное дерево
4) Лепнина, многоуровневые потолки, глянец и тяжёлые шторы с ламбрекенами
5) Сплошной тик: дерево на полу, стенах, мебели и потолке одного тона — нужен контраст светлых стен
6) Только винтаж без современной эргономики (кухни, хранение) — стиль ценил функциональность

Допущения и предложения на листе. Основа листа: размеры сняты со скана обмерного плана KV оформление (см): часть подписей не читается, помещения выровнены по читаемым размерам; контрольный обмер не выполнен (К-1); высота потолка 2650 мм принята по отметкам обмера (Н = 2,50…2,66 м, ригель 2,28 м) — уточнить при обмере (К-2); толщины стен 300 / 120 мм приняты, межквартирная стена и колонны — по скану, не замерены (К-1); разрешённая мощность 15 кВт принята по типовым ТУ; при объединении двух квартир — переоформление ТУ (К-4); подрайон климата не задан — принят не северный (жилые от 2,5 м) (К-8). См. лист открытых вопросов (лист 6, записи К-1, К-2, К-4, К-8).

## Примечания

1. Коды цвета — по веерам производителей (колерная карта, лист 57); перед закупкой краски — выкрас на стене объекта под дневным светом и лампами проекта.
2. Материалы — по ведомости отделки (лист 54); мебель, текстиль и декор — по спецификации (лист 20). Образцы доски, керамогранита и тканей утвердить до заказа.
3. Фактуры на листе условные, цвет передан по HEX-значениям производителей: при печати возможны отклонения, решение — только по физическому образцу.

| Изм. | Кол.уч | Лист | № док. | Подп. | Дата |
|---|---|---|---|---|---|
| Разраб. | | Кырлан А.С. | | | 04.11.26 |
| Пров. | | | | | |
| ГИП | | | | | |
| | | | | | |
| Н. контр. | | | | | |
| Утв. | | | | | |

**ГД-2026-009-АИ**

Квартира 103 м²

Общая площадь 100,72* м² · * размеры со скана, не замерены (реестр — л. 6, 7, К-1)

Дизайн-проект интерьера

| Стадия | Лист | Листов |
|---|---|---|
| РП | 18 | 120 |


**Концепция интерьера**
М б/м

**Кырлан Александр Сергеевич**

выпуск 04.11.2026 № 35b47f1c2a · стр. 20 из 130

# План расстановки мебели

Мебель и оборудование · размеры в мм от чистовых стен · марки — по ведомости

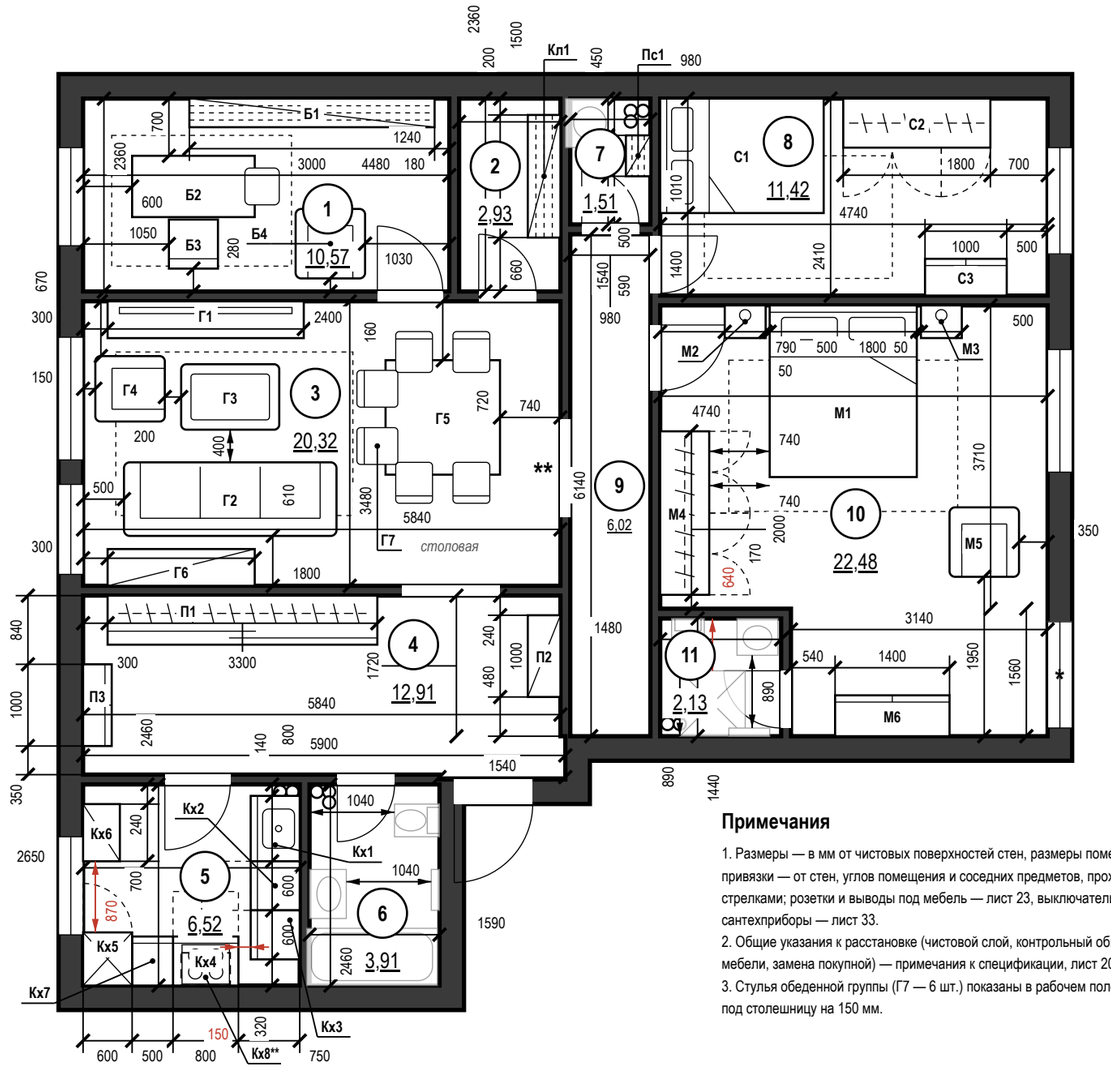


## Примечания

1. Размеры — в мм от чистовых поверхностей стен, размеры помещений — в свету, привязки — от стен, углов помещения и соседних предметов, проходы и зазоры стрелками; розетки и выводы под мебель — лист 23, выключатели — лист 25, сантехприборы — лист 33.
2. Общие указания к расстановке (чистовой слой, контрольный обмер, зазоры встроенной мебели, замена покупной) — примечания к спецификации, лист 20.
3. Стулья обеденной группы (Г7 — 6 шт.) показаны в рабочем положении, задвинутыми под столешницу на 150 мм.

## Условные обозначения

- мебель и оборудование — габарит в масштабе
- навесные шкафы (низ выше 0,9 м) — невидимый контур
- ковёр
- зона открывания дверец шкафов и техники
- К1 — марка предмета по ведомости мебели
- привязка от чистовой стены, мм
- ширина прохода, зазор, мм
- проход меньше нормы — расстановку изменить
- сантехприборы — подложка (лист ВК)
- существующие стены (сечение)
- * — «*» — принято, не замерено и не подтверждено
- ** — «**» — предложение проектировщика, заказчиком не утверждено
- стояк: К1 — канализация, В1 — ХВС, Т3 — ГВС
- 1 — номер помещения, площадь м²
- *зона* — функциональная зона помещения

**Допущения и предложения на листе**

Основа листа: размеры сняты со скана обмерного плана KV оформление (см): часть подписей не читается, помещения выровнены по читаемым размерам; контрольный обмер не выполнен (К-1); высота потолка 2650 мм принята по отметкам обмера (Н = 2,50…2,66 м, ригель 2,28 м) — уточнить при обмере (К-2); толщины стен 300 / 120 мм приняты, межквартирная стена и колонны — по скану, не замерены (К-1); разрешённая мощность 15 кВт принята по типовым ТУ; при объединении двух квартир — переоформление ТУ (К-4); подрайон климата не задан — принят не северный (жилые от 2,5 м) (К-8).
Знак «*» — принято, не замерено и не подтверждено (замерить на объекте): К-1: окно пом. 10 (стена Б) — Окно 1300 при смещение 3500 на стене Б основной части (длина 3830) выходило за стену на 970 мм; К-6: Ст К1-3, Ст В1-3, Ст Т3-3 — положение снято со скана обмера, отдельно не замерялось; ось внутри габарита поддона См1 — обмер угла по К-6.
Знак «**» — предложение проектировщика, заказчиком не утверждено (согласовать с заказчиком): Кх8 — над индукционной панелью Кх4 нужна вытяжка: в составе кухни её не было, розетка вытяжки образца висела без потребителя; К-5: дверь пом. 3 (стена Б) — проём в межквартирной стене — объединение квартир, предложение до техзаключения.
Открытые вопросы и конфликты по листу: К-1.
См. лист открытых вопросов (лист 6, записи К-1, К-2, К-4–К-6, К-8).

1000 мм · печать 1:1

**ПРЕДВАРИТЕЛЬНО · не для производства работ · открыто пунктов: 8 (реестр — л. 6, 7)**

**Экспликация помещений**

лист 14 · на плане — номера в марках

## Ведомость мебели и оборудования

| Марка | Наименование | Ш×Г×В, мм | Пом. | Кол. |
|---|---|---|---|---|
| Б1 | Стеллаж-библиотека из ореха | 3000×350×2400 | 1 | 1 |
| Б2 | Письменный стол-бюро середины века | 750×1500×750 | 1 | 1 |
| Б3 | Стул рабочий с подлокотниками | 600×600×800 | 1 | 1 |
| Б4 | Кресло-лаунж с оттоманкой | 850×850×850 | 1 | 1 |
| Кл1 | Стеллаж для хранения | 1500×400×2400 | 2 | 1 |
| Г1 | ТВ-консоль из ореха | 2400×450×550 | 3 | 1 |
| Г2 | Диван середины века | 2600×900×780 | 3 | 1 |
| Г3 | Стол журнальный | 1200×800×400 | 3 | 1 |
| Г4 | Кресло | 800×850×1070 | 3 | 1 |
| Г5 | Стол обеденный на одной ножке | 1400×1400×730 | 3 | 1 |
| Г6 | Буфет-сервант из ореха | 1800×450×750 | 3 | 1 |
| П1 | Шкаф-купе | 3300×600×2450 | 4 | 1 |
| П2 | Банкетка | 1000×400×450 | 4 | 1 |
| П3 | Консоль ар-деко | 1000×350×800 | 4 | 1 |
| Кх1 | Модуль под мойку | 800×600×900 | 5 | 1 |
| Кх2 | Посудомоечная машина встроенная | 600×600×900 | 5 | 1 |
| Кх3 | Модуль с ящиками | 600×600×900 | 5 | 1 |
| Кх4 | Модуль с варочной панелью | 800×600×900 | 5 | 1 |
| Кх7 | Модуль с ящиками между | 500×600×900 | 5 | 1 |
| Кх5 | Колонна с холодильником | 600×650×2100 | 5 | 1 |
| Кх6 | Стол барный у окна | 700×450×900 | 5 | 1 |
| Кх8** | Вытяжка над варочной панелью | 600×400×600 | 5 | 1 |
| Пс1 | Полки для хранения | 500×300×2000 | 7 | 1 |
| С1 | Кровать 1400×2000 | 1400×2000×450 | 8 | 1 |
| С2 | Шкаф распашной | 1800×600×2400 | 8 | 1 |
| С3 | Туалетный столик середины века | 1000×450×750 | 8 | 1 |
| М1 | Кровать 1800×2100 | 1800×2100×450 | 10 | 1 |
| М2 | Тумба прикроватная | 500×400×550 | 10 | 1 |
| М3 | Тумба прикроватная | 500×400×550 | 10 | 1 |
| М4 | Шкаф распашной | 2000×600×2400 | 10 | 1 |
| М5 | Кресло-лаунж с оттоманкой | 850×850×850 | 10 | 1 |
| М6 | Комод ар-деко | 1400×500×800 | 10 | 1 |
| Г7 | Стул обеденный к столу Г5 | 450×500×820 | 3 | 6 |

Ш — вдоль стены (изголовья), Г — от стены (длина кровати)
Материалы, модели, допуск замены — лист 20

| Изм. | Кол.уч | Лист | № док. | Подп. | Дата |
|---|---|---|---|---|---|
| Разраб. | | Кырлан А.С. | | | 04.11.26 |
| Пров. | | | | | |
| ГИП | | | | | |
| | | | | | |
| Н. контр. | | | | | |
| Утв. | | | | | |

**ГД-2026-009-АИ**

Квартира 103 м²

Общая площадь 100,72* м² · * размеры со скана, не замерены (реестр — л. 6, 7, К-1)

Дизайн-проект интерьера

| Стадия | Лист | Листов |
|---|---|---|
| РП | 19 | 120 |

**План расстановки мебели**

М 1:75

**Кырлан Александр Сергеевич**

выпуск 04.11.2026 № 35b47f1c2a · стр. 21 из 130

# Спецификация мебели и оборудования

**ПРЕДВАРИТЕЛЬНО · не для производства работ · открыто пунктов: 8 (реестр — л. 6, 7)**

Форма 1 ГОСТ 21.110-2013 · позиции мебели — по плану расстановки

| Поз. | Наименование и техническая характеристика | Тип, марка, обозначение документа, опросного листа | Код продукции | Поставщик | Ед. измерения | Кол. | Масса 1 ед., кг | Примечание |
|---|---|---|---|---|---|---|---|---|
| | **Мебель встроенная и корпусная (изготовление по чертежам мебельщика)** | | | | | | | |
| Кл1 | Стеллаж для хранения; каркас и полки — ЛДСП декор «орех» 16 мм; без фасадов; Ш×Г×В 1500×400×2400 мм | | | изготовление на заказ | шт. | 1 | | пом. 2 |
| П1 | Шкаф-купе; корпус ЛДСП 16 мм; фасады — МДФ, шпон ореха 10 мм, масло матовое в профиле: латунь; Ш×Г×В 3300×600×2450 мм | | | изготовление на заказ | шт. | 1 | | пом. 4 |
| Кх1 | Модуль под мойку; корпус ЛДСП 16 мм; фасады — МДФ, шпон ореха 18 мм, масло матовое; Ш×Г×В 800×600×900 мм | | | изготовление на заказ | шт. | 1 | | пом. 5 |
| Кх2 | Модуль под встраиваемую ПММ 60; без корпуса (ниша между соседними модулями); фасад на дверь машины — МДФ 18 мм, эмаль матовая; цоколь; цвет фасадов — в цвет стен (Farrow & Ball No. 291); Ш×Г×В 600×600×900 мм | | | изготовление на заказ | шт. | 1 | | пом. 5 |
| Кх3 | Модуль с ящиками; корпус ЛДСП 16 мм; фасады — МДФ 18 мм, эмаль матовая; цвет фасадов — в цвет стен (Farrow & Ball No. 291); Ш×Г×В 600×600×900 мм | | | изготовление на заказ | шт. | 1 | | пом. 5 |
| Кх4 | Модуль с варочной панелью (индукция) и духовым шкафом; корпус ЛДСП 16 мм; фасады — МДФ 18 мм, эмаль матовая; цвет фасадов — в цвет стен (Farrow & Ball No. 291); Ш×Г×В 800×600×900 мм | | | изготовление на заказ | шт. | 1 | | пом. 5 |
| Кх5 | Колонна с холодильником, ретро-фасад; корпус ЛДСП 16 мм; фасады — МДФ эмаль 18 мм, матовая; цвет — тил; Ш×Г×В 600×650×2100 мм | | | изготовление на заказ | шт. | 1 | | пом. 5 |
| Кх7 | Модуль с ящиками между колонной и плитой; корпус ЛДСП 16 мм; фасады — МДФ 18 мм, эмаль матовая; цвет фасадов — в цвет стен (Farrow & Ball No. 291); Ш×Г×В 500×600×900 мм | | | изготовление на заказ | шт. | 1 | | пом. 5 |
| Кх8** | Вытяжка над варочной панелью; корпус ЛДСП 16 мм; фасады — МДФ 18 мм, эмаль матовая; цвет фасадов — в цвет стен (Farrow & Ball No. 291); Ш×Г×В 600×400×600 мм | | | изготовление на заказ | шт. | 1 | | пом. 5 |
| Пс1 | Полки для хранения (стена Б, в стороне от короба стояков); каркас и полки — ЛДСП 16 мм, декор «дуб натуральный»; без фасадов; Ш×Г×В 500×300×2000 мм | | | изготовление на заказ | шт. | 1 | | пом. 7 |
| С2 | Шкаф распашной, латунные ручки; корпус ЛДСП 16 мм; фасады — МДФ, шпон ореха 18 мм, масло матовое; Ш×Г×В 1800×600×2400 мм | | | изготовление на заказ | шт. | 1 | | пом. 8 |
| М4 | Шкаф распашной; корпус ЛДСП 16 мм; фасады — МДФ, шпон ореха 18 мм, масло матовое; вставка — латунь; Ш×Г×В 2000×600×2400 мм | | | изготовление на заказ | шт. | 1 | | пом. 10 |
| | **Мебель покупная** | | | | | | | |
| Б1 | Стеллаж-библиотека из ореха на всю стену, латунные полкодержатели; шпон, дуб натуральный, матовое масло; Ш×Г×В 3000×350×2400 мм | | | аналог по характеристикам | шт. | 1 | | пом. 1; замена ≤ габарита |
| Б2 | Письменный стол-бюро середины века, орех, конические ножки; шпон, дуб натуральный, матовое масло; Ш×Г×В 750×1500×750 мм | | | аналог по характеристикам | шт. | 1 | | пом. 1; замена ≤ габарита |
| Б3 | Стул рабочий с подлокотниками, гнутая фанера и кожа; обивка — ткань, цвет Farrow & Ball No. 298; каркас — дуб натуральный; Ш×Г×В 600×600×800 мм | | | аналог по характеристикам | шт. | 1 | | пом. 1; замена ≤ габарита |
| Б4 | Кресло-лаунж с оттоманкой (в духе Eames Lounge Chair), палисандровый шпон, чёрная кожа; обивка — ткань, цвет Farrow & Ball No. 298; Ш×Г×В 850×850×850 мм | | | аналог по характеристикам | шт. | 1 | | пом. 1; замена ≤ габарита |
| Г1 | ТВ-консоль из ореха на конических ножках, ТВ на стене; шпон, дуб натуральный, матовое масло; Ш×Г×В 2400×450×550 мм | | | аналог по характеристикам | шт. | 1 | | пом. 3; замена ≤ габарита |
| Г2 | Диван середины века (в духе Florence Knoll), букле горчичного цвета, латунные опоры; обивка — ткань, цвет Farrow & Ball No. 298; Ш×Г×В 2600×900×780 мм | | | аналог по характеристикам | шт. | 1 | | пом. 3; замена ≤ габарита |
| Г3 | Стол журнальный (в духе Noguchi Coffee Table), орех и стекло; шпон, дуб натуральный, матовое масло; Ш×Г×В 1200×800×400 мм | | | аналог по характеристикам | шт. | 1 | | пом. 3; замена ≤ габарита |
| Г4 | Кресло (в духе Egg Chair), изумрудный бархат; обивка — ткань, цвет Farrow & Ball No. 298; Ш×Г×В 800×850×1070 мм | | | аналог по характеристикам | шт. | 1 | | пом. 3; замена ≤ габарита |
| Г5 | Стол обеденный на одной ножке (в духе Tulip Table), мрамор Calacatta, d 1400; шпон, дуб натуральный, матовое масло; Ш×Г×В 1400×1400×730 мм | | | аналог по характеристикам | шт. | 1 | | пом. 3; замена ≤ габарита |
| Г6 | Буфет-сервант из ореха на конических ножках, раздвижные двери; шпон, дуб натуральный, матовое масло; Ш×Г×В 1800×450×750 мм | | | аналог по характеристикам | шт. | 1 | | пом. 3; замена ≤ габарита |
| Г7 | Стул обеденный к столу Г5; обивка — ткань, цвет Farrow & Ball No. 298; каркас — дуб натуральный; Ш×Г×В 450×500×820 мм | | | аналог по характеристикам | шт. | 6 | | пом. 3; замена ≤ габарита |
| П2 | Банкетка, изумрудный бархат, латунные ножки; Ш×Г×В 1000×400×450 мм | | | аналог по характеристикам | шт. | 1 | | пом. 4; замена ≤ габарита |
| П3 | Консоль ар-деко, чёрный лак и латунь; шпон, дуб натуральный, матовое масло; Ш×Г×В 1000×350×800 мм | | | аналог по характеристикам | шт. | 1 | | пом. 4; замена ≤ габарита |

## Примечания

1. Позиции мебели совпадают с марками на плане расстановки (лист 19); размеры Ш×Г×В — Ш вдоль стены, Г от стены.
2. Размеры и привязки плана расстановки — в мм от чистовых поверхностей стен: слой штукатурки 20 мм по блоку и 5 мм шпаклёвки по ГКЛ учтён; привязки — от стен и углов помещения, а не от другой мебели.
3. План расстановки не является документацией для изготовления мебели. Встроенная и корпусная мебель изготавливается по чертежам мебельщика после контрольного обмера (после штукатурки); «стена в стену» — с зазором 10 мм с каждой стороны или с компенсаторами; графы «Тип, марка» и «Код продукции» для неё не заполняются (ГОСТ 21.110-2013).
4. Покупные изделия — аналог по характеристикам: заменять только на изделия не больше указанного габарита и того же материала и цвета.
5. Материал и цвет, не указанные в данных изделия, приняты по концепции (лист 18): тон дерева — по полу, обивка — по вторичному цвету палитры; образцы согласовать до заказа.
6. Масса 1 ед. для изделий до 25 кг не указывается. Техника — по монтажным схемам изготовителя; выводы — по листам ЭОМ и ВК.

Допущения и предложения на листе. Знак «**» предложено (согласовать). См. лист открытых вопросов (лист 6).

| Изм. | Кол.уч | Лист | № док. | Подп. | Дата |
|---|---|---|---|---|---|
| Разраб. | | Кырлан А.С. | | | 04.11.26 |
| Пров. | | | | | |
| ГИП | | | | | |
| | | | | | |
| Н. контр. | | | | | |
| Утв. | | | | | |

**ГД-2026-009-АИ**

Квартира 103 м²

Общая площадь 100,72* м² · * размеры со скана, не замерены (реестр — л. 6, 7, К-1)

| Дизайн-проект интерьера | Стадия | Лист | Листов |
|---|---|---|---|
| | РП | 20 | 120 |

**Спецификация мебели и оборудования**

М б/м

**Кырлан Александр Сергеевич**

# Спецификация мебели и оборудования (продолжение)



Форма 1 ГОСТ 21.110-2013 · позиции мебели — по плану расстановки

| Поз. | Наименование и техническая характеристика | Тип, марка, обозначение документа, опросного листа | Код продукции | Поставщик | Ед. измерения | Кол. | Масса 1 ед., кг | Примечание |
|---|---|---|---|---|---|---|---|---|
| Кх6 | Стол барный у окна, терраццо; Ш×Г×В 700×450×900 мм | | | аналог по характеристикам | шт. | 1 | | пом. 5; замена ≤ габарита |
| С1 | Кровать 1400×2000, изголовье с каннелюрами, бархат цвета тил; мягкое изголовье, обивка — ткань, цвет Farrow & Ball No. 298; Ш×Г×В 1400×2000×450 мм | | | аналог по характеристикам | шт. | 1 | | пом. 8; замена ≤ габарита |
| С3 | Туалетный столик середины века с круглым зеркалом; шпон, дуб натуральный, матовое масло; Ш×Г×В 1000×450×750 мм | | | аналог по характеристикам | шт. | 1 | | пом. 8; замена ≤ габарита |
| М1 | Кровать 1800×2100 с высоким изголовьем ар-деко, изумрудный бархат, латунный кант; мягкое изголовье, обивка ткань, цвет Farrow & Ball No. 298; Ш×Г×В 1800×2100×450 мм | | | аналог по характеристикам | шт. | 1 | | пом. 10; замена ≤ габарита |
| М2, М3 | Тумба прикроватная, орех и латунь; шпон, дуб натуральный, матовое масло; Ш×Г×В 500×400×550 мм | | | аналог по характеристикам | шт. | 2 | | пом. 10; замена ≤ габарита |
| М5 | Кресло-лаунж с оттоманкой (в духе Eames Lounge Chair), коньячная кожа; обивка — ткань, цвет Farrow & Ball No. 298; Ш×Г×В 850×850×850 мм | | | аналог по характеристикам | шт. | 1 | | пом. 10; замена ≤ габарита |
| М6 | Комод ар-деко, макассар и латунь; шпон, дуб натуральный, матовое масло; Ш×Г×В 1400×500×800 мм | | | аналог по характеристикам | шт. | 1 | | пом. 10; замена ≤ габарита |
| | **Техника встраиваемая и бытовая (покупные изделия), светильники под розетки** | | | | | | | |
| | Посудомоечная машина встраиваемая, в модуле Кх2; ниша 600 мм | аналог по характеристикам: полновстраиваемая 60 см под фасад, ниша 600 × 862 мм, навеска фасада в комплекте | | по выбору заказчика до изготовления мебели | шт. | 1 | | пом. 5; по схеме изготовителя |
| | Духовой шкаф встраиваемый, в модуле Кх4 | аналог по характеристикам: 60 см, лицевая панель 595 мм, ниша 560 × 600, глубина ≥ 550 мм, вентиляция за прибором | | по выбору заказчика до изготовления мебели | шт. | 1 | | пом. 5; по схеме изготовителя |
| | Варочная панель встраиваемая, индукционная, в модуле Кх4 | аналог по характеристикам: индукционная 60 см, вырез 560 × 490 мм по шаблону модели | | по выбору заказчика до изготовления мебели | шт. | 1 | | пом. 5; по схеме изготовителя |
| | Холодильник встраиваемый, в модуле Кх5 | аналог по характеристикам: полновстраиваемый под фасад, ниша 1780 × 560 × 550 мм, вентиляция решётка в цоколе, выход сверху | | по выбору заказчика до изготовления мебели | шт. | 1 | | пом. 5; по схеме изготовителя |
| | Вытяжка, в модуле Кх8** | аналог по характеристикам: производительность — по расчёту ОВ, шум ≤ 55 дБ(А) | | по выбору заказчика до изготовления мебели | шт. | 1 | | пом. 5; по схеме изготовителя |
| | Стиральная машина, место по листу ВК (Пм1); Ш×Г 600×600 мм | аналог по характеристикам: тип загрузки — по листу ВК, в плане 600 × 600 мм (ширина × глубина), по листу ВК | | по выбору заказчика до изготовления мебели | шт. | 1 | | пом. 7; по схеме изготовителя |
| | Торшер, у поз. Г6; абажур — ткань или опаловое стекло; лампа 2700 K | | | аналог по характеристикам | шт. | 1 | | пом. 3; розетка Р3 (ЭОМ) |
| | **Текстиль** | | | | | | | |
| Т7 | Портьеры-волна; лён 100 %; цвет NCS S 1005-Y20R; карниз 1820 мм, высота 2640 мм, сборка 2 | | | аналог по характеристикам | шт. | 2 | | пом. 1 |
| Т8 | Тюль; полиэстер 100 %; цвет NCS S 0502-Y; карниз 1820 мм, высота 2640 мм, сборка 2,5 | | | аналог по характеристикам | шт. | 1 | | пом. 1 |
| Т9 | Ковёр под рабочей зоной, геометрия середины века; шерсть 100 %; цвет NCS S 2050-Y20R; 2200×1600 мм | | | аналог по характеристикам | шт. | 1 | | пом. 1; с подложкой |
| Т10 | Подушки декоративные на кровать; букле (шерсть 60 %, полиэстер 40 %); цвет NCS S 3050-Y70R | | | аналог по характеристикам | шт. | 3 | | пом. 1 |
| Т12 | Плед на кровать; шерсть мериноса 100 %; цвет Farrow & Ball No. 289 | | | аналог по характеристикам | шт. | 1 | | пом. 1 |
| Т1 | Портьеры-волна, два полотна; лён 100 %; цвет NCS S 1005-Y20R; карниз 2150 мм, высота 2640 мм, сборка 2 | | | аналог по характеристикам | шт. | 2 | | пом. 3 |
| Т2 | Тюль-вуаль, одно полотно; полиэстер 100 %; цвет Farrow & Ball No. 291; карниз 2150 мм, высота 2640 мм, сборка 2,5 | | | аналог по характеристикам | шт. | 1 | | пом. 3 |
| Т3 | Ковёр мягкой группы, абстрактная геометрия середины века; шерсть 100 %; цвет Farrow & Ball No. 298; 2900×2000 мм | | | аналог по характеристикам | шт. | 1 | | пом. 3; с подложкой |
| Т4 | Подушки декоративные на диван; лён 100 %; цвет NCS S 1005-Y20R | | | аналог по характеристикам | шт. | 3 | | пом. 3 |

**Допущения и предложения на листе**

Основа листа: размеры сняты со скана обмерного плана KV оформление (см): часть подписей не читается, помещения выровнены по читаемым размерам; контрольный обмер не выполнен (К-1); высота потолка 2650 мм принята по отметкам обмера (Н = 2,50…2,66 м, ригель 2,28 м) — уточнить при обмере (К-2); толщины стен 300 / 120 мм приняты, межквартирная стена и колонны — по скану, не замерены (К-1); разрешённая мощность 15 кВт принята по типовым ТУ; при объединении двух квартир — переоформление ТУ (К-4); подрайон климата не задан — принят не северный (жилые от 2,5 м) (К-8).

Знак «**» — предложение проектировщика, заказчиком не утверждено (согласовать с заказчиком): Кх8 — над индукционной панелью Кх4 нужна вытяжка: в составе кухни её не было, розетка вытяжки образца висела без потребителя.

См. лист открытых вопросов (лист 6, записи К-1, К-2, К-4, К-8).

| Изм. | Кол.уч | Лист | № док. | Подп. | Дата |
|---|---|---|---|---|---|
| Разраб. | | Кырлан А.С. | | | 04.11.26 |
| Пров. | | | | | |
| ГИП | | | | | |
| | | | | | |
| Н. контр. | | | | | |
| Утв. | | | | | |

**ГД-2026-009-АИ**

Квартира 103 м²

Общая площадь 100,72* м² · * размеры со скана, не замерены (реестр — л. 6, 7, К-1)

Дизайн-проект интерьера

| Стадия | Лист | Листов |
|---|---|---|
| РП | 21 | 120 |

**Спецификация мебели и оборудования (продолжение)**

М б/м

**Кырлан Александр Сергеевич**

# Спецификация мебели и оборудования (продолжение)

Форма 1 ГОСТ 21.110-2013 · позиции мебели — по плану расстановки

**ПРЕДВАРИТЕЛЬНО · не для производства работ · открыто пунктов: 8 (реестр — л. 6, 7)**

| Поз. | Наименование и техническая характеристика | Тип, марка, обозначение документа, опросного листа | Код продукции | Поставщик | Ед. измерения | Кол. | Масса 1 ед., кг | Примечание |
|---|---|---|---|---|---|---|---|---|
| Т5 | Подушки декоративные на диван, акцент; хлопковый бархат 100 %; цвет Farrow & Ball No. 255 | | | аналог по характеристикам | шт. | 2 | | пом. 3 |
| Т6 | Плед на диван; шерсть мериноса 100 %; цвет Farrow & Ball No. 255 | | | аналог по характеристикам | шт. | 1 | | пом. 3 |
| Т14 | Рулонная штора кассетная, ткань димаут; полиэстер 100 %; цвет NCS S 1005-Y20R; карниз 1600 мм, высота 1750 мм | | | аналог по характеристикам | шт. | 1 | | пом. 5 |
| Т11 | Портьеры-волна; лён 100 %; цвет NCS S 1005-Y20R; карниз 1820 мм, высота 2640 мм, сборка 2 | | | аналог по характеристикам | шт. | 2 | | пом. 8 |
| Т13 | Тюль; полиэстер 100 %; цвет NCS S 0502-Y; карниз 1820 мм, высота 2640 мм, сборка 2,5 | | | аналог по характеристикам | шт. | 1 | | пом. 8 |
| Т15 | Ковёр под кроватью; шерсть 100 %; цвет NCS S 2050-Y20R; 2300×1500 мм | | | аналог по характеристикам | шт. | 1 | | пом. 8; с подложкой |
| Т16 | Подушки декоративные на кровать; букле (шерсть 60 %, полиэстер 40 %); цвет NCS S 3050-Y70R | | | аналог по характеристикам | шт. | 3 | | пом. 8 |
| Т17 | Подушки на кровать, акцент; хлопковый бархат 100 %; цвет NCS S 5030-B10G | | | аналог по характеристикам | шт. | 2 | | пом. 8 |
| Т18 | Плед на кровать; шерсть мериноса 100 %; цвет Farrow & Ball No. 289 | | | аналог по характеристикам | шт. | 1 | | пом. 8 |
| Т19 | Портьеры-волна; лён 100 %; цвет NCS S 1005-Y20R; карниз 2500 мм, высота 2640 мм, сборка 2 | | | аналог по характеристикам | шт. | 2 | | пом. 10 |
| Т20 | Тюль; полиэстер 100 %; цвет NCS S 0502-Y; карниз 2500 мм, высота 2640 мм, сборка 2,5 | | | аналог по характеристикам | шт. | 1 | | пом. 10 |
| Т21 | Ковёр под кроватью; шерсть 80 %, хлопок 20 %; цвет Farrow & Ball No. 298; 2800×1850 мм | | | аналог по характеристикам | шт. | 1 | | пом. 10; с подложкой |
| Т22 | Подушки декоративные на кровать; лён 100 %; цвет NCS S 1005-Y20R | | | аналог по характеристикам | шт. | 3 | | пом. 10 |
| Т23 | Подушки на кровать, акцент; хлопковый бархат 100 %; цвет Farrow & Ball No. 289 | | | аналог по характеристикам | шт. | 2 | | пом. 10 |
| Т24 | Плед на кровать; шерсть мериноса 100 %; цвет Farrow & Ball No. 289 | | | аналог по характеристикам | шт. | 1 | | пом. 10 |
| | **Декор** | | | | | | | |
| ДК3 | Картина над креслом: графика середины века, рама — орех; 1000×700 мм; низ на 1100 мм от пола | | | аналог по характеристикам | шт. | 1 | 4 | пом. 1; крепление к стене |
| ДК1 | Картина над буфетом: абстракция середины века, рама — латунь; 1200×900 мм; низ на 1000 мм от пола | | | аналог по характеристикам | шт. | 1 | 6 | пом. 3; крепление: планка на дюбелях, 4 точки |
| ДК2 | Фикус лировидный в кашпо Ø400; 450×450 мм | | | аналог по характеристикам | шт. | 1 | | пом. 3 |
| ДК5 | Зеркало; рама — чёрный матовый; 800×1800 мм; низ на 550 мм от пола | | | аналог по характеристикам | шт. | 1 | 18 | пом. 4; крепление: анкер, 4 шт. |
| ДК8 | Часы настенные Ø400; 400×400 мм; центр на 1550 мм от пола | | | аналог по характеристикам | шт. | 1 | 2 | пом. 5; крепление: дюбель с крюком, 1 точка |
| ДК9 | Хлорофитум хохлатый на подоконнике (отм. +0,800); 300×200 мм; низ на 800 мм от пола | | | аналог по характеристикам | шт. | 1 | | пом. 5 |
| ДК4 | Картина над кроватью: графика в паспарту, рама — дуб; 1000×700 мм; низ на 1100 мм от пола | | | аналог по характеристикам | шт. | 1 | 4 | пом. 8; крепление к стене |
| ДК6 | Зеркало в рост в тонкой чёрной раме; рама — чёрный матовый; 600×1600 мм; низ на 300 мм от пола | | | аналог по характеристикам | шт. | 1 | 12 | пом. 8; крепление: анкер для пустотелых оснований, 4 шт. |
| ДК7 | Картина над кроватью: абстракция, холст, тонкая рама из дуба; 1200×700 мм; низ на 1300 мм от пола | | | аналог по характеристикам | шт. | 1 | 4 | пом. 10; крепление к стене |

**Допущения и предложения на листе**

Основа листа: размеры сняты со скана обмерного плана KV оформление (см): часть подписей не читается, помещения выровнены по читаемым размерам; контрольный обмер не выполнен (К-1); высота потолка 2650 мм принята по отметкам обмера (Н = 2,50…2,66 м, ригель 2,28 м) — уточнить при обмере (К-2); толщины стен 300 / 120 мм приняты, межквартирная стена и колонны — по скану, не замерены (К-1); разрешённая мощность 15 кВт принята по типовым ТУ; при объединении двух квартир — переоформление ТУ (К-4); подрайон климата не задан — принят не северный (жилые от 2,5 м) (К-8).

См. лист открытых вопросов (лист 6, записи К-1, К-2, К-4, К-8).

| Изм. | Кол.уч | Лист | № док. | Подп. | Дата |
|---|---|---|---|---|---|
| Разраб. | | Кырлан А.С. | | | 04.11.26 |
| Пров. | | | | | |
| ГИП | | | | | |
| | | | | | |
| Н. контр. | | | | | |
| Утв. | | | | | |

**ГД-2026-009-АИ**

Квартира 103 м²

Общая площадь 100,72* м² · * размеры со скана, не замерены (реестр — л. 6, 7, К-1)

Дизайн-проект интерьера

| Стадия | Лист | Листов |
|---|---|---|
| РП | 22 | 120 |

**Спецификация мебели и оборудования (продолжение)**

М б/м

**Кырлан Александр Сергеевич**

03

# Электрооборудование


Кырлан Александр Сергеевич

выпуск 04.11.2026 № 35b47f1c2a · стр. 25 из 130

# План розеток и электровыводов

Розетки, выводы кабеля, щит · размеры в мм · высоты от чистого пола

**ПРЕДВАРИТЕЛЬНО · не для производства работ · открыто пунктов: 8 (реестр — л. 6, 7)**

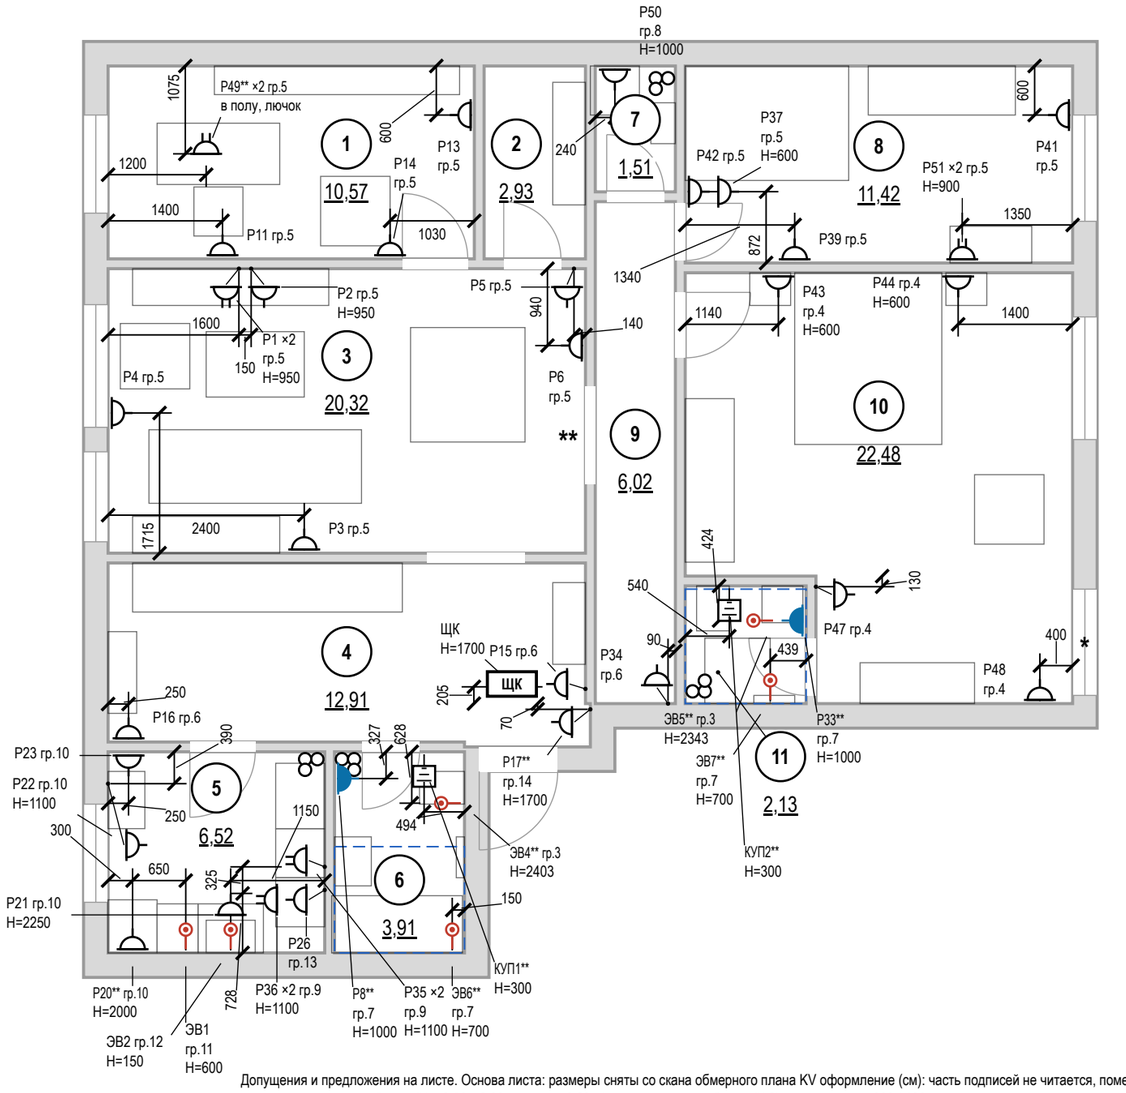


## Условные обозначения

| Знак | Тип изделия | H, мм | Кол., шт |
|---|---|---|---|
| | Розетка с заземлением | 300 | 17 |
| | То же | у знака | 9 |
| | Блок розеток с заземлением, рамка 2 поста | у знака | 5 |
| | Розетка с заземлением IP44 | 1000 | 2 |
| | Вывод кабеля к прибору | у знака | 6 |
| | КУП (уравнивание потенциалов) | 300 | 2 |
| ЩК | Щит квартирный | 1700 | 1 |

розетка с заземляющим контактом; у знака — марка, ×N — постов в рамке, гр. — группа щита, H — высота оси, мм

знак разведён для читаемости: точка на стене — у выноски, привязка — до неё

граница зоны 2 ванной (600 мм от ванны/поддона)

мебель и сантехприборы — подложка

стояк: К1 — канализация, В1 — ХВС, Т3 — ГВС

1 — номер помещения, площадь м²

**Итого розеток (механизмов) — 38 шт; рамок — 33 шт: на 1 пост — 28, на 2 поста — 5.**

Допущения и предложения на листе. Основа листа: размеры сняты со скана обмерного плана KV оформление (см): часть подписей не читается, помещения выровнены по читаемым размерам; контрольный обмер не выполнен (К-1); высота потолка 2650 мм принята по отметкам обмера (H = 2,50…2,66 м, ригель 2,28 м) — уточнить при обмере (К-2); толщины стен 300 / 120 мм приняты, межквартирная стена и колонны — по скану, не замерены (К-1); разрешённая мощность 15 кВт принята по типовым ТУ; при объединении двух квартир — переоформление ТУ (К-4); подрайон климата не задан — принят не северный (жилые от 2,5 м) (К-8). Знак «*» — принято, не замерено (замерить): К-6: Ст К1-3, Ст В1-3, Ст Т3-3. Знак «**» — предложено, не утверждено (согласовать): P49, P17, P20, КУП1, ЭВ5, КУП2; ИЗ-1: P8, ЭВ4, ЭВ6, P33, ЭВ7. См. лист открытых вопросов (лист 6, записи ИЗ-1, К-1, К-2, К-4–К-6, К-8).

## Примечания

1. За отметку 0,000 принят уровень чистого пола. Высоты H — от чистого пола до оси изделия; привязки — от чистовой грани стены до оси механизма (у рамки на несколько постов — до оси рамки).
2. Розетки без отметки H у знака — на высоте 300 мм от чистого пола до оси механизма; выводы кабеля — по паспорту прибора.
3. Розетки в санузле — только вне зон 0–2 (ПУЭ 7.1.48, ГОСТ Р 50571.7.701-2024), IP44, через УЗО 30 мА.
4. Розеточные и мокрые линии — через УЗО или дифавтомат с током утечки не более 30 мА (ПУЭ 7.1.79); в санузле выполнить ДСУП (ПУЭ 7.1.87–7.1.88).
5. Кабель — медный, исполнение нг(А)-LS (ГОСТ 31565-2012); скрытая прокладка только горизонтально и вертикально, фактические трассы зафиксировать исполнительной схемой до закрытия отделкой.
6. Расчёт нагрузок, токов КЗ, селективности и сечений — по проекту ЭОМ организации с допуском СРО; лист задаёт состав, расположение и группы.
7. Выводы кухонной техники — после утверждения проекта кухни (ориентировочно); привязки выводов даны от осей модулей гарнитура и пересматриваются вместе с проектом кухни.
8. Электрический тёплый пол проектом не предусмотрен; при решении заказчика устроить — отдельный лист «План тёплых полов»: контуры с отступом 100 мм от стен и мебели без ножек, датчик в гофре, терморегулятор, своя группа щита через УЗО 30 мА.
9. Ведомости электроточек, изделий, светильников и расшифровка клавиш — лист 26.

1000 мм · печать 1:1

| Изм. | Кол.уч | Лист | № док. | Подп. | Дата |
|---|---|---|---|---|---|
| Разраб. | | Кырлан А.С. | | | 04.11.26 |
| Пров. | | | | | |
| ГИП | | | | | |
| Н. контр. | | | | | |
| Утв. | | | | | |

**ГД-2026-009-АИ**

Квартира 103 м²

Общая площадь 100,72* м² · * размеры со скана, не замерены (реестр — л. 6, 7, К-1)

Дизайн-проект интерьера

| Стадия | Лист | Листов |
|---|---|---|
| РП | 23 | 120 |

**План розеток и электровыводов**

М 1:75


**Кырлан Александр Сергеевич**

выпуск 04.11.2026 № 35b47f1c2a · стр. 26 из 130

# План освещения

Светильники, группы включения, извещатели · размеры в мм



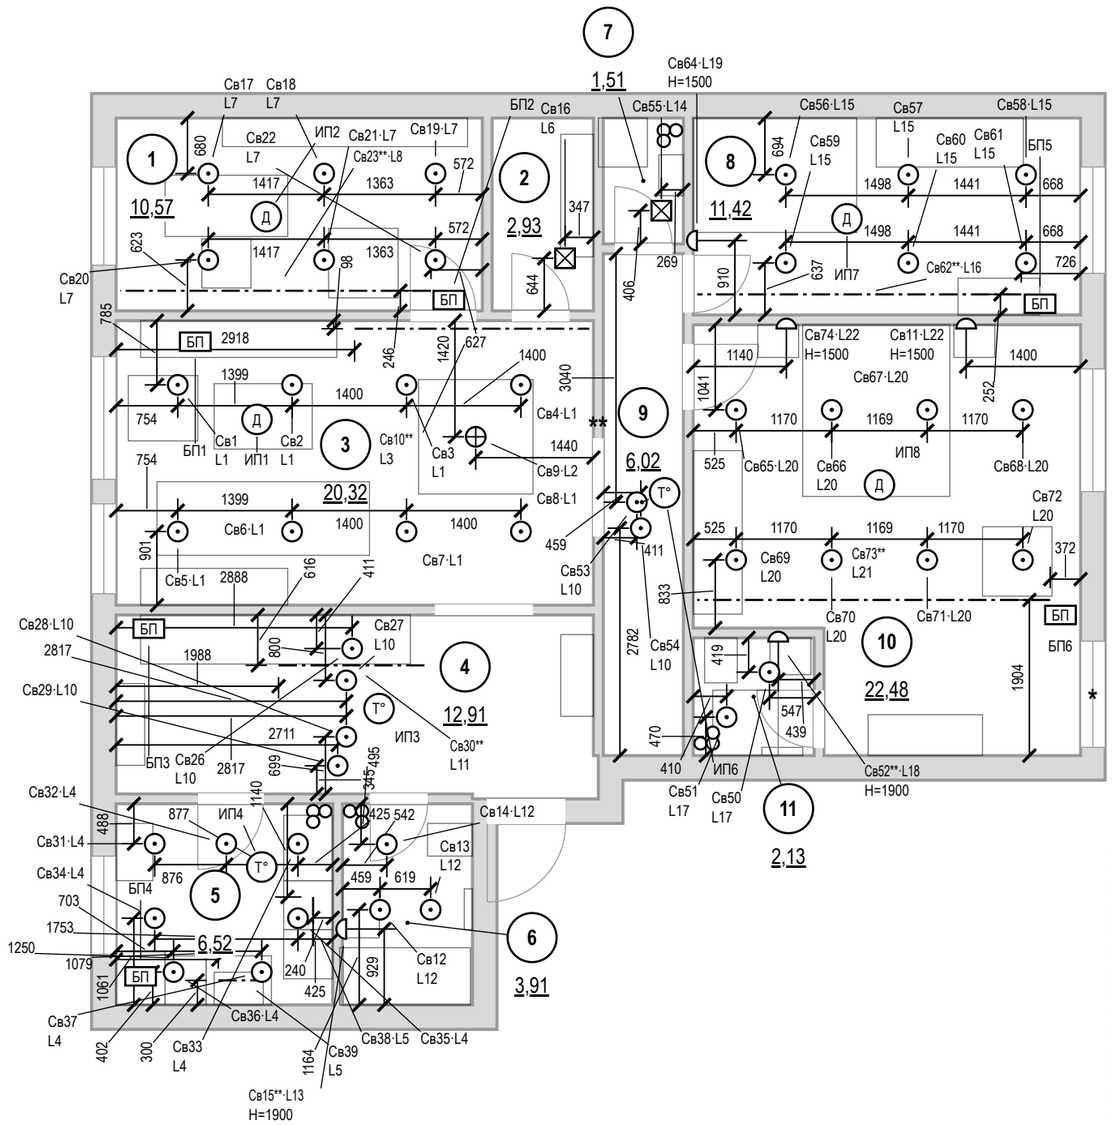


## Условные обозначения

- светильник встраиваемый точечный
- светильник потолочный накладной
- светильник подвесной
- светильник настенный (бра), H — высота оси
- светодиодная лента в профиле / в карнизе короба
- Св1·L1 — марка светильника (как в ведомости и на развёртках) · группа включения L (лист 25)
- Д — извещатель пожарный дымовой автономный
- Т° — извещатель пожарный тепловой
- БП — блок питания LED, с доступом (люк от 100×100 мм)
- мебель и сантехприборы — подложка
- стояк: К1 — канализация, В1 — ХВС, Т3 — ГВС
- 1 — номер помещения, площадь м²

**Допущения и предложения на листе**

Основа листа: размеры сняты со скана обмерного плана KV оформление (см): часть подписей не читается, помещения выровнены по читаемым размерам; контрольный обмер не выполнен (К-1); высота потолка 2650 мм принята по отметкам обмера (H = 2,50…2,66 м, ригель 2,28 м) — уточнить при обмере (К-2); толщины стен 300 / 120 мм приняты, межквартирная стена и колонны — по скану, не замерены (К-1); разрешённая мощность 15 кВт принята по типовым ТУ; при объединении двух квартир — переоформление ТУ (К-4); подрайон климата не задан — принят не северный (жилые от 2,5 м) (К-8).

Знак «*» — принято, не замерено и не подтверждено (замерить на объекте): К-1: окно пом. 10 (стена Б) — Окно 1300 при смещение 3500 на стене Б основной части (длина 3830) выходило за стену на 970 мм; К-6: Ст К1-3, Ст В1-3, Ст Т3-3 — положение снято со скана обмера, отдельно не замерялось; ось внутри габарита поддона См1 — обмер угла по К-6.

Знак «**» — предложение проектировщика, заказчиком не утверждено (согласовать с заказчиком): Св23, Св10, Св30, Св62, Св73 — открытая лента в накладном профиле вместо «в коробе»: короба в потолке нет — высота 2650 мм < 2700 — один уровень (табл. 1.3); Св15 — Сдвиг под раскладку плитки стены Г на 141 мм вдоль стены — ось на шве или в центре плитки, привязка по таблице листа; Св52 — свет у зеркала — над зеркалом у умывальника по его оси (свет на лицо, а не над сантехникой); сдвиг под раскладку плитки стены А на 149 мм вдоль стены — ось на шве или в центре плитки, привязка по таблице листа; К-5: дверь пом. 3 (стена Б) — проём в межквартирной стене — объединение квартир, предложение до техзаключения. См. лист открытых вопросов (лист 6, записи К-1, К-2, К-4–К-6, К-8).

## Примечания

1. За отметку 0,000 принят уровень чистого пола. Высоты H — от чистого пола до оси изделия; привязки — от чистовой грани стены до оси механизма (у рамки на несколько постов — до оси рамки).
2. Высота установки, не указанная на плане: светильники — на потолке; настенные — по отметке H у знака. Привязки — до оси светильника от чистовой грани стены, по рядам.
3. Во влажных помещениях — светильники не ниже IP44; в зонах 0–2 ванной — по ГОСТ Р 50571.7.701-2024 (зона 1 — IPX5).
4. Розеточные и мокрые линии — через УЗО или дифавтомат с током утечки не более 30 мА (ПУЭ 7.1.79); в санузле выполнить ДСУП (ПУЭ 7.1.87–7.1.88).
5. Кабель — медный, исполнение нг(A)-LS (ГОСТ 31565-2012); скрытая прокладка только горизонтально и вертикально, фактические трассы зафиксировать исполнительной схемой до закрытия отделкой.
6. Расчёт нагрузок, токов КЗ, селективности и сечений — по проекту ЭОМ организации с допуском СРО; лист задаёт состав, расположение и группы.
7. Ведомость светильников (тип, количество, мощность, поток, Tц, Ra) — лист 43.
8. Оценка освещённости (по норме СанПиН 1.2.3685-21, табл. 5.52, на полу; не светотехнический расчёт, декоративная подсветка в оценку не входит) — лист 26.

1000 мм · печать 1:1

| Изм. | Кол.уч | Лист | № док. | Подп. | Дата |
|---|---|---|---|---|---|
| Разраб. | | Кырлан А.С. | | | 04.11.26 |
| Пров. | | | | | |
| ГИП | | | | | |
| Н. контр. | | | | | |
| Утв. | | | | | |

**ГД-2026-009-АИ**

Квартира 103 м²

Общая площадь 100,72* м² · * размеры со скана, не замерены (реестр — л. 6, 7, К-1)

Дизайн-проект интерьера

| Стадия | Лист | Листов |
|---|---|---|
| РП | 24 | 120 |

**План освещения**

М 1:75


**Кырлан Александр Сергеевич**

выпуск 04.11.2026 № 35b47f1c2a · стр. 27 из 130

# План выключателей и схема включения

Выключатели S, группы включения L, линии связи · размеры в мм

**ПРЕДВАРИТЕЛЬНО · не для производства работ · открыто пунктов: 8 (реестр — л. 6, 7)**

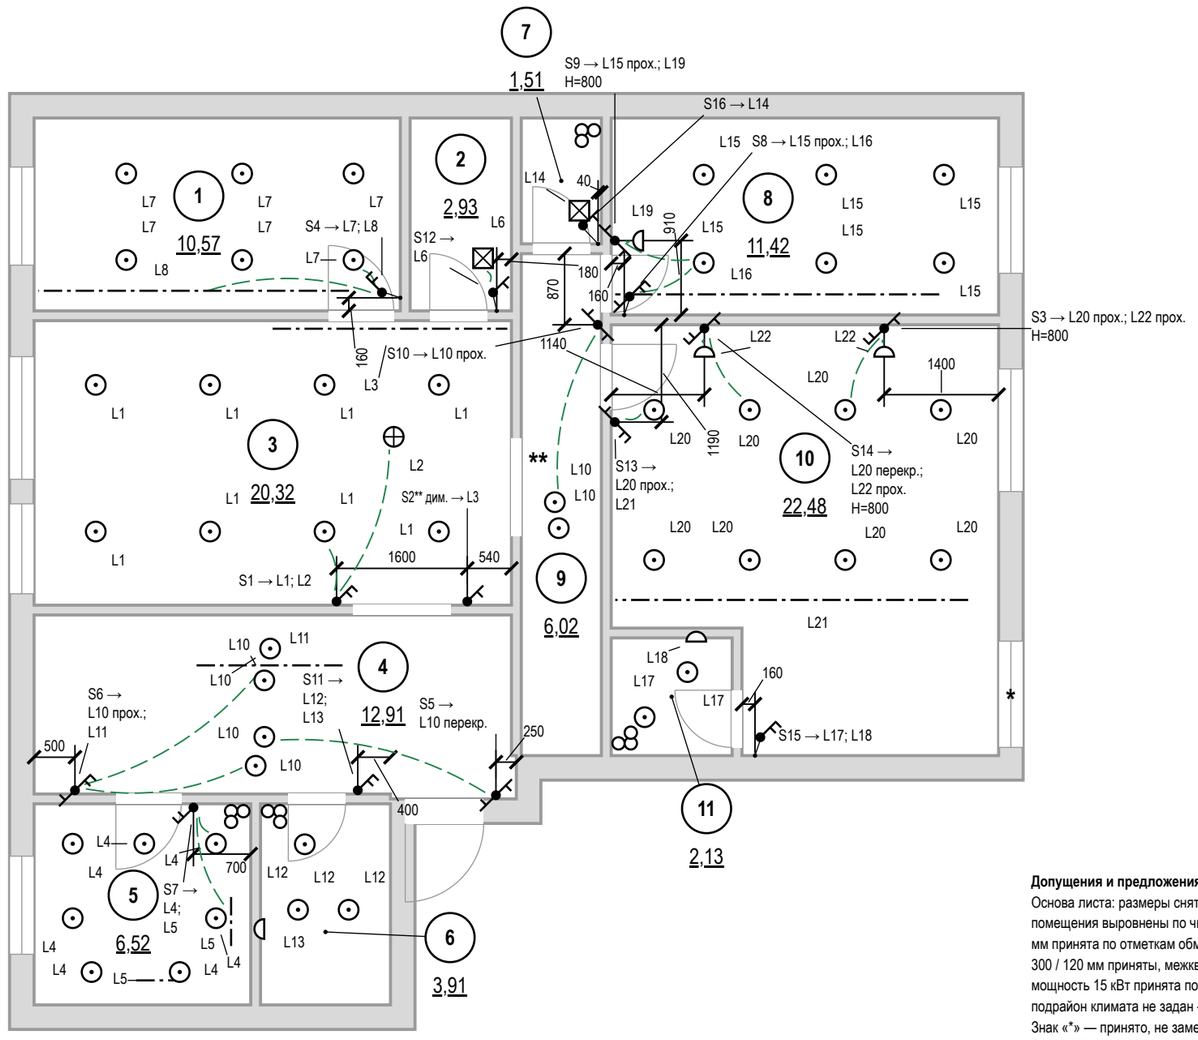


## Условные обозначения

- выключатель одноклавишный
- выключатель двухклавишный (флажков — по числу клавиш)
- выключатель с проходной или перекрёстной клавишей (обратный флажок); тип клавиши — в подписи
- S1 → — марка → группы по клавишам (через «;»): прох. — проходной, перекр. — перекрёстный, дим. — светорегулятор; Н — высота
- связь: выключатель → ближайший светильник группы в том же помещении (не трасса кабеля); полный состав группы — по номеру L
- светильник встраиваемый точечный
- светильник потолочный накладной
- светильник подвесной
- светильник настенный (бра), Н — высота оси
- светодиодная лента в профиле / в карнизе короба
- L1 — группа включения у светильника
- стояк: К1 — канализация, В1 — ХВС, Т3 — ГВС
- 1 — номер помещения, площадь м²

**Допущения и предложения на листе**

Основа листа: размеры сняты со скана обмерного плана KV оформление (см): часть подписей не читается, помещения выровнены по читаемым размерам; контрольный обмер не выполнен (К-1); высота потолка 2650 мм принята по отметкам обмера (Н = 2,50…2,66 м, ригель 2,28 м) — уточнить при обмере (К-2); толщины стен 300 / 120 мм приняты, межквартирная стена и колонны — по скану, не замерены (К-1); разрешённая мощность 15 кВт принята по типовым ТУ; при объединении двух квартир — переоформление ТУ (К-4); подрайон климата не задан — принят не северный (жилые от 2,5 м) (К-8).

Знак «*» — принято, не замерено и не подтверждено (замерить на объекте): К-1: окно пом. 10 (стена Б) — Окно 1300 при смещение 3500 на стене Б основной части (длина 3830) выходило за стену на 970 мм; К-6: Ст К1-3, Ст В1-3, Ст Т3-3 — положение снято со скана обмера, отдельно не замерялось; ось внутри габарита поддона См1 — обмер угла по К-6.

Знак «**» — предложение проектировщика, заказчиком не утверждено (согласовать с заказчиком): S2 — светорегулятор добавлен под диммируемую ленту L3; уровни сценариев выбраны конвейером; К-5: дверь пом. 3 (стена Б) — проём в межквартирной стене — объединение квартир, предложение до техзаключения. См. лист открытых вопросов (лист 6, записи К-1, К-2, К-4–К-6, К-8).

## Примечания

1. За отметку 0,000 принят уровень чистого пола. Высоты Н — от чистого пола до оси изделия; привязки — от чистовой грани стены до оси механизма (у рамки на несколько постов — до оси рамки).
2. Высота установки, не указанная на плане: выключатели — 900 мм от чистого пола (у кровати и другие — Н у марки), со стороны дверной ручки (ПУЭ 7.1.51).
3. Какой выключатель какие светильники включает — по номеру группы L: у выключателя (S1 → L1; L2 — клавиши по порядку) и у каждого светильника. Пунктир подсказка к ближайшему светильнику группы в том же помещении (не дальше 3 м), это не трасса кабеля; выключатель за стеной (у двери санузла) и далёкая группа — только номер группы.
4. Группы из нескольких мест (L10 — S5, S6, S10; L15 — S8, S9; L20 — S3, S13, S14; L22 — S3, S14): на крайних местах — проходные клавиши, на промежуточных перекрёстные; механизмы — в ведомости изделий.
5. Светорегулятор — по заднему фронту (для LED-драйверов), совместимость с драйверами проверить до закупки.
6. Розеточные и мокрые линии — через УЗО или дифавтомат с током утечки не более 30 мА (ПУЭ 7.1.79); в санузле выполнить ДСУП (ПУЭ 7.1.87–7.1.88).
7. Кабель — медный, исполнение нг(А)-LS (ГОСТ 31565-2012); скрытая прокладка только горизонтально и вертикально, фактические трассы зафиксировать исполнительной схемой до закрытия отделкой.
8. Расчёт нагрузок, токов КЗ, селективности и сечений — по проекту ЭОМ организации с допуском СРО; лист задаёт состав, расположение и группы.
9. Расшифровка клавиш и ведомость изделий — лист 26.

1000 мм · печать 1:1

| Изм. | Кол.уч | Лист | № док. | Подп. | Дата |
|---|---|---|---|---|---|
| Разраб. | | Кырлан А.С. | | | 04.11.26 |
| Пров. | | | | | |
| ГИП | | | | | |
| Н. контр. | | | | | |
| Утв. | | | | | |

**ГД-2026-009-АИ**

Квартира 103 м²

Общая площадь 100,72* м² · * размеры со скана, не замерены (реестр — л. 6, 7, К-1)

Дизайн-проект интерьера

| Стадия | Лист | Листов |
|---|---|---|
| РП | 25 | 120 |

**План выключателей и схема включения**

М 1:75

**Кырлан Александр Сергеевич**

выпуск 04.11.2026 № 35b47f1c2a · стр. 28 из 130

# Ведомость электроточек и изделий

Электроточки, изделия, светильники, освещённость, клавиши выключателей · б/м

## Ведомость электроточек

| Марка | Пом. | Назначение | Н, мм | Гр. |
|---|---|---|---|---|
| Р11 | 1 | общего назначения | 300 | 5 |
| Р13 | 1 | уборка | 300 | 5 |
| Р14 | 1 | уборка у входа | 300 | 5 |
| Р49** | 1 | рабочий стол — лючок в полу под столом | 0 | 5 |
| Р1 | 3 | ТВ-зона: телевизор, медиаплеер | 950 | 5 |
| Р2 | 3 | ТВ-зона: саундбар | 950 | 5 |
| Р3 | 3 | торшер у дивана Г2 | 300 | 5 |
| Р4 | 3 | кресло у окна Г4 | 300 | 5 |
| Р5 | 3 | обеденная зона, буфет Г6 | 300 | 5 |
| Р6 | 3 | уборка | 300 | 5 |
| Р15 | 4 | пылесос, сушилка обуви | 300 | 6 |
| Р16 | 4 | уборка | 300 | 6 |
| Р17** | 4 | питание слаботочного щита (рядом с ЩС**) | 1700 | 14 |
| ЩК | 4 | щит квартирный ЩРВ-П-48 | 1700 | |
| Р20** | 5 | холодильник — над нишей, съёмная панель | 2000 | 10 |
| Р21 | 5 | вытяжка — над корпусом | 2250 | 10 |
| Р22 | 5 | барный стол Кх6: мелкая техника | 1100 | 10 |
| Р23 | 5 | уборка | 300 | 10 |
| Р26 | 5 | посудомоечная машина — в соседнем модуле, за ящиком | 300 | 13 |
| Р35 | 5 | фартук | 1100 | 9 |
| Р36 | 5 | фартук | 1100 | 9 |
| ЭВ1 | 5 | варочная панель — в соседнем модуле, за ящиком | 600 | 11 |
| ЭВ2 | 5 | духовой шкаф — в цоколе | 150 | 12 |
| КУП1** | 6 | КУП — уравнивание потенциалов (ДСУП) | 300 | |
| Р8** | 6 | фен у умывальника, IP44 | 1000 | 7 |
| ЭВ4** | 6 | вентилятор ВР1 (таймер выбега) | 2403 | 3 |
| ЭВ6** | 6 | полотенцесушитель П10, IP44 | 700 | 7 |
| Р50 | 7 | стиральная машина | 1000 | 8 |
| Р37 | 8 | у кровати | 600 | 5 |
| Р39 | 8 | общего назначения | 300 | 5 |

## Ведомость электроточек (продолжение)

| Марка | Пом. | Назначение | Н, мм | Гр. |
|---|---|---|---|---|
| Р41 | 8 | уборка | 300 | 5 |
| Р42 | 8 | уборка у входа | 300 | 5 |
| Р51 | 8 | туалетный столик: фен, подсветка зеркала | 900 | 5 |
| Р34 | 9 | уборка | 300 | 6 |
| Р43 | 10 | у кровати | 600 | 4 |
| Р44 | 10 | у кровати | 600 | 4 |
| Р47 | 10 | общего назначения | 300 | 4 |
| Р48 | 10 | уборка | 300 | 4 |
| КУП2** | 11 | КУП — уравнивание потенциалов (ДСУП) | 300 | |
| Р33** | 11 | фен у умывальника, IP44 | 1000 | 7 |
| ЭВ5** | 11 | вентилятор ВР3 (таймер выбега) | 2343 | 3 |
| ЭВ7** | 11 | полотенцесушитель П13, IP44 | 700 | 7 |

## Ведомость изделий

| Наименование | Марки | Ед. | Кол. |
|---|---|---|---|
| Розетка с з/к и защитными шторками, 16 А | по ведомости точек | шт | 36 |
| Розетка IP44 с крышкой, 16 А | Р8**, Р33** | шт | 2 |
| Выключатель 1-клав. | S12, S16 | шт | 2 |
| Выключатель 1-клав. перекрёстный | S5 | шт | 1 |
| Выключатель 1-клав. проходной | S10 | шт | 1 |
| Выключатель 2-клав. | S1, S4, S7, S11, S15 | шт | 5 |
| Выключатель 2-клав. (перекрёстная + проходная) | S14 | шт | 1 |
| Выключатель 2-клав. (проходная + обычная) | S6, S8, S9, S13 | шт | 4 |
| Выключатель 2-клав. проходной | S3 | шт | 1 |
| Светорегулятор 1-канальный, задний фронт (LED) | S2** | шт | 1 |
| Датчик движения ночной подсветки | L11 | шт | 1 |
| Рамка 1-постовая | в т. ч. 16 под выключ. | шт | 44 |
| Рамка 2-постовая | | шт | 5 |
| Коробка установочная (подрозетник) Ø68 | розетки, выключатели | шт | 54 |

## Ведомость изделий (продолжение)

| Наименование | Марки | Ед. | Кол. |
|---|---|---|---|
| Вывод кабеля под прибор (клеммник) | ЭВ1, ЭВ2, ЭВ4**, ЭВ5**, ЭВ6**, ЭВ7** | шт | 6 |
| Коробка уравнивания потенциалов КУП | КУП1**, КУП2** | шт | 2 |
| Блок питания LED 24 В, 200 Вт, дим. | БП2, БП5, БП6 | шт | 3 |
| Блок питания LED 24 В, 100 Вт, дим. | БП1 | шт | 1 |
| Блок питания LED 24 В, 20 Вт | БП3 | шт | 1 |
| Блок питания LED 24 В, 30 Вт | БП4 | шт | 1 |
| Извещатель дымовой автономный | ИП1, ИП2, ИП7, ИП8 | шт | 4 |
| Извещатель тепловой | ИП3, ИП4, ИП6 | шт | 3 |
| Щит квартирный (состав — лист щита) | ЩК | шт | 1 |
| Розетка компьютерная RJ45, кат. 6, с рамкой и подрозетником | LAN1, LAN3, LAN4, LAN5** | шт | 4 |
| Розетка телевизионная (коаксиальная) с рамкой и подрозетником | ТВ1 | шт | 1 |
| Точка доступа Wi-Fi (оборудование заказчика), питание PoE | АР1** | шт | 1 |
| Трубка или монитор домофона (поставка домофонной организации) | ДФ1 | шт | 1 |
| Щит слаботочный ЩС**: корпус, DIN-рейка, розетки 220 В | ЩС** | шт | 1 |
| Патч-панель, портов не менее 5 | | шт | 1 |
| Коммутатор, портов не менее 5, из них PoE 1 | | шт | 1 |
| Кабель домофона — тип по системе поставщика (по лучам от ЩС**, запас 10 %) | | м | 4,3 |
| Кабель коаксиальный RG-6 (75 Ом) к розеткам ТВ (по лучам от ЩС**, запас 10 %) | | м | 16,1 |
| Кабель U/UTP кат. 6 (LAN, Wi-Fi и камеры по PoE) (по лучам от ЩС**, запас 10 %) | | м | 70,3 |

Допущения и предложения на листе. Основа листа: размеры сняты со скана обмерного плана KV оформление (см): часть подписей не читается, помещения выровнены по читаемым размерам; контрольный обмер не выполнен (К-1); высота потолка 2650 мм принята по отметкам обмера (Н = 2,50…2,66 м, ригель 2,28 м) — уточнить при обмере (К-2); толщины стен 300 / 120 мм приняты, межквартирная стена и колонны — по скану, не замерены (К-1); разрешённая мощность 15 кВт принята по типовым ТУ; при объединении двух квартир — переоформление ТУ (К-4); подрайон климата не задан — принят не северный (жилые от 2,5 м) (К-8). Знак «**» — предложено, не утверждено (согласовать): Св23, Р49, LAN5, S2, Св10, Р17, Св30, Р20, Св15, КУП1, Св62, Св73, Св52, ЭВ5, КУП2, ЩС, АР1; ИЗ-1: Р8, ЭВ4, ЭВ6, Р33, ЭВ7. См. лист открытых вопросов (лист 6, записи ИЗ-1, К-1, К-2, К-4, К-8).

## Ведомость светильников

| Поз. | Марки | Тип | Кол. | Р, Вт | Ф, лм | IP | Тц/Ra |
|---|---|---|---|---|---|---|---|
| 1 | Св17–Св22, Св56–Св61 | встраиваемый точечный | 12 | 12 | 1050 | | 2700/90 |
| 2 | Св23**, Св62** | светодиодная лента, 12,3 м | 2 | 118,1 | 11070 | | 2700/90 |
| 3 | Св16, Св55 | потолочный накладной | 2 | 10 | 900 | | 3000/90 |
| 4 | Св1–Св8, Св31–Св37 | встраиваемый точечный | 15 | 12 | 1000 | | 3000/90 |
| 5 | Св9 | подвесной | 1 | 15 | 1200 | | 2700/90 |
| 6 | Св10** | светодиодная лента, 5,4 м | 1 | 51,8 | 4860 | | 2700/90 |
| 7 | Св26–Св29, Св53, Св54 | встраиваемый точечный | 6 | 7 | 600 | | 3000/90 |
| 8 | Св30** | светодиодная лента, 1,8 м | 1 | 8,6 | 270 | | 2700/90 |
| 9 | Св38, Св39 | линейный светильник | 2 | 8 | 700 | | 3000/90 |
| 10 | Св12–Св14, Св51 | встраиваемый точечный | 4 | 6 | 500 | 44 | 3000/90 |
| 11 | Св15**, Св52** | настенный (бра), Н=1900 | 2 | 8 | 600 | 44 | 3000/90 |
| 12 | Св11, Св64, Св74 | настенный (бра), Н=1500 | 3 | 6 | 400 | | 2700/90 |
| 13 | Св65–Св72 | встраиваемый точечный | 8 | 12 | 1000 | | 2700/90 |
| 14 | Св73** | светодиодная лента, 15,5 м | 1 | 148,8 | 13950 | | 2700/90 |
| 15 | Св50 | встраиваемый точечный | 1 | 7 | 600 | 44 | 3000/90 |

## Освещённость (оценка)

| Пом. | S, м² | Ен, лк | Ф треб., лм | Ф по пр., лм |
|---|---|---|---|---|
| 1 | 10,6 | 300 | 8930 | 6300 |
| 2 | 2,9 | 30 | 250 | 900 |
| 3 | 20,3 | 150 | 8590 | 8000 |
| 4 | 12,9 | 50 | 1820 | 2400 |
| 5 | 6,5 | 150 | 2750 | 7000 |
| 6 | 3,9 | 50 | 550 | 1500 |
| 7 | 1,5 | 75 | 320 | 900 |
| 8 | 11,4 | 150 | 4830 | 6300 |

## Примечания

1. Ведомости сведены с планов розеток, освещения и выключателей; марки, группы и высоты — те же, что у знаков на планах.
2. Механизмы, рамки и светорегуляторы — одной серии; число постов и клавиш сверено с выбранной серией. Перекрёстная клавиша — отдельный механизм серии.
3. Освещённость (оценка) — по норме СанПиН 1.2.3685-21 (табл. 5.52, на полу), не светотехнический расчёт; декоративная подсветка в оценку не входит.
4. За отметку 0,000 принят уровень чистого пола. Высоты Н — от чистого пола до оси изделия; привязки — от чистовой грани стены до оси механизма (у рамки на несколько постов — до оси рамки).
5. Розеточные и мокрые линии — через УЗО или дифавтомат с током утечки не более 30 мА (ПУЭ 7.1.79); в санузле выполнить ДСУП (ПУЭ 7.1.87–7.1.88).
6. Кабель — медный, исполнение нг(А)-LS (ГОСТ 31565-2012); скрытая прокладка только горизонтально и вертикально, фактические трассы зафиксировать исполнительной схемой до закрытия отделкой.
7. Расчёт нагрузок, токов КЗ, селективности и сечений — по проекту ЭОМ организации с допуском СРО; лист задаёт состав, расположение и группы.
8. Ведомости занимают 2 листов этого наименования: таблицы, не вошедшие в поле листа, продолжены на следующем листе.

| Изм. | Кол.уч | Лист | № док. | Подп. | Дата |
|---|---|---|---|---|---|
| Разраб. | | Кырлан А.С. | | | 04.11.26 |
| Пров. | | | | | |
| ГИП | | | | | |
| | | | | | |
| Н. контр. | | | | | |
| Утв. | | | | | |

**ГД-2026-009-АИ**

Квартира 103 м²

Общая площадь 100,72* м² · * размеры со скана, не замерены (реестр — л. 6, 7, К-1)

Дизайн-проект интерьера

| Стадия | Лист | Листов |
|---|---|---|
| РП | 26 | 120 |

**Ведомость электроточек и изделий**

М б/м

**Кырлан Александр Сергеевич**

выпуск 04.11.2026 № 35b47f1c2a · стр. 29 из 130

# Ведомость электроточек и изделий (продолжение)

Электроточки, изделия, светильники, освещённость, клавиши выключателей · б/м

### Освещённость (оценка) (продолжение)

| Пом. | S, м² | Ен, лк | Ф треб., лм | Ф по пр., лм |
|---|---|---|---|---|
| 9 | 6 | 50 | 850 | 1200 |
| 10 | 22,5 | 150 | 9500 | 8000 |
| 11 | 2,1 | 50 | 300 | 1100 |

### Расшифровка клавиш

| Марка | Пом. | H, мм | Клав. | Механизм | Группа: светильники |
|---|---|---|---|---|---|
| S1 | 3 | 900 | 1 | обычный | L1: Св1–Св8 |
| | | | 2 | обычный | L2: Св9 |
| S2** | 3 | 900 | 1 | светорегулятор | L3: Св10** |
| S3 | 10 | 800 | 1 | проходной | L20: Св65–Св72 |
| | | | 2 | проходной | L22: Св11, Св74 |
| S4 | 1 | 900 | 1 | обычный | L7: Св17–Св22 |
| | | | 2 | обычный | L8: Св23** |
| S5 | 4 | 900 | 1 | перекрёстный | L10: Св26–Св29, Св53, Св54 |
| S6 | 4 | 900 | 1 | проходной | L10: Св26–Св29, Св53, Св54 |
| | | | 2 | обычный | L11: Св30** |
| S7 | 5 | 900 | 1 | обычный | L4: Св31–Св37 |
| | | | 2 | обычный | L5: Св38, Св39 |
| S8 | 8 | 900 | 1 | проходной | L15: Св56–Св61 |
| | | | 2 | обычный | L16: Св62** |
| S9 | 8 | 800 | 1 | проходной | L15: Св56–Св61 |
| | | | 2 | обычный | L19: Св64 |
| S10 | 9 | 900 | 1 | проходной | L10: Св26–Св29, Св53, Св54 |
| S11 | 4 | 900 | 1 | обычный | L12: Св12–Св14 |
| | | | 2 | обычный | L13: Св15** |
| S12 | 2 | 900 | 1 | обычный | L6: Св16 |
| S13 | 10 | 900 | 1 | проходной | L20: Св65–Св72 |
| | | | 2 | обычный | L21: Св73** |
| S14 | 10 | 800 | 1 | перекрёстный | L20: Св65–Св72 |
| | | | 2 | проходной | L22: Св11, Св74 |
| S15 | 10 | 900 | 1 | обычный | L17: Св50, Св51 |
| | | | 2 | обычный | L18: Св52** |
| S16 | 7 | 900 | 1 | обычный | L14: Св55 |

**Допущения и предложения на листе**

Основа листа: размеры сняты со скана обмерного плана KV оформление (см): часть подписей не читается, помещения выровнены по читаемым размерам; контрольный обмер не выполнен (К-1); высота потолка 2650 мм принята по отметкам обмера (H = 2,50…2,66 м, ригель 2,28 м) — уточнить при обмере (К-2); толщины стен 300 / 120 мм приняты, межквартирная стена и колонны — по скану, не замерены (К-1); разрешённая мощность 15 кВт принята по типовым ТУ; при объединении двух квартир — переоформление ТУ (К-4); подрайон климата не задан — принят не северный (жилые от 2,5 м) (К-8).

Знак «**» — предложение проектировщика, заказчиком не утверждено (согласовать с заказчиком): Св23, Св10, Св30, Св62, Св73 — открытая лента в накладном профиле вместо «в коробе»: короба в потолке нет — высота 2650 мм < 2700 — один уровень (табл. 1.3); S2 — светорегулятор добавлен под диммируемую ленту L3; уровни сценариев выбраны конвейером; Св15 — Сдвиг под раскладку плитки стены Г на 141 мм вдоль стены — ось на шве или в центре плитки, привязка по таблице листа; Св52 — свет у зеркала — над зеркалом у умывальника по его оси (свет на лицо, а не над сантехникой); сдвиг под раскладку плитки стены А на 149 мм вдоль стены — ось на шве или в центре плитки, привязка по таблице листа.

См. лист открытых вопросов (лист 6, записи К-1, К-2, К-4, К-8).

### Примечания

1. Продолжение ведомостей: лист 2 из 2 этого наименования; таблицы, прерванные на предыдущем листе, продолжены с заголовком «(продолжение)».
2. За отметку 0,000 принят уровень чистого пола. Высоты H — от чистого пола до оси изделия; привязки — от чистовой грани стены до оси механизма (у рамки на несколько постов — до оси рамки).
3. Розеточные и мокрые линии — через УЗО или дифавтомат с током утечки не более 30 мА (ПУЭ 7.1.79); в санузле выполнить ДСУП (ПУЭ 7.1.87–7.1.88).
4. Кабель — медный, исполнение нг(A)-LS (ГОСТ 31565-2012); скрытая прокладка только горизонтально и вертикально, фактические трассы зафиксировать исполнительной схемой до закрытия отделкой.
5. Расчёт нагрузок, токов КЗ, селективности и сечений — по проекту ЭОМ организации с допуском СРО; лист задаёт состав, расположение и группы.

| Изм. | Кол.уч | Лист | № док. | Подп. | Дата |
|---|---|---|---|---|---|
| Разраб. | | Кырлан А.С. | | | 04.11.26 |
| Пров. | | | | | |
| ГИП | | | | | |
| | | | | | |
| Н. контр. | | | | | |
| Утв. | | | | | |

**ГД-2026-009-АИ**

Квартира 103 м²

Общая площадь 100,72* м² · * размеры со скана, не замерены (реестр — л. 6, 7, К-1)

Дизайн-проект интерьера

| Стадия | Лист | Листов |
|---|---|---|
| РП | 27 | 120 |

**Ведомость электроточек и изделий (продолжение)**


М б/м

**Кырлан Александр Сергеевич**

выпуск 04.11.2026 № 35b47f1c2a · стр. 30 из 130

# Однолинейная схема щита

Щит квартирный ЩК · без масштаба

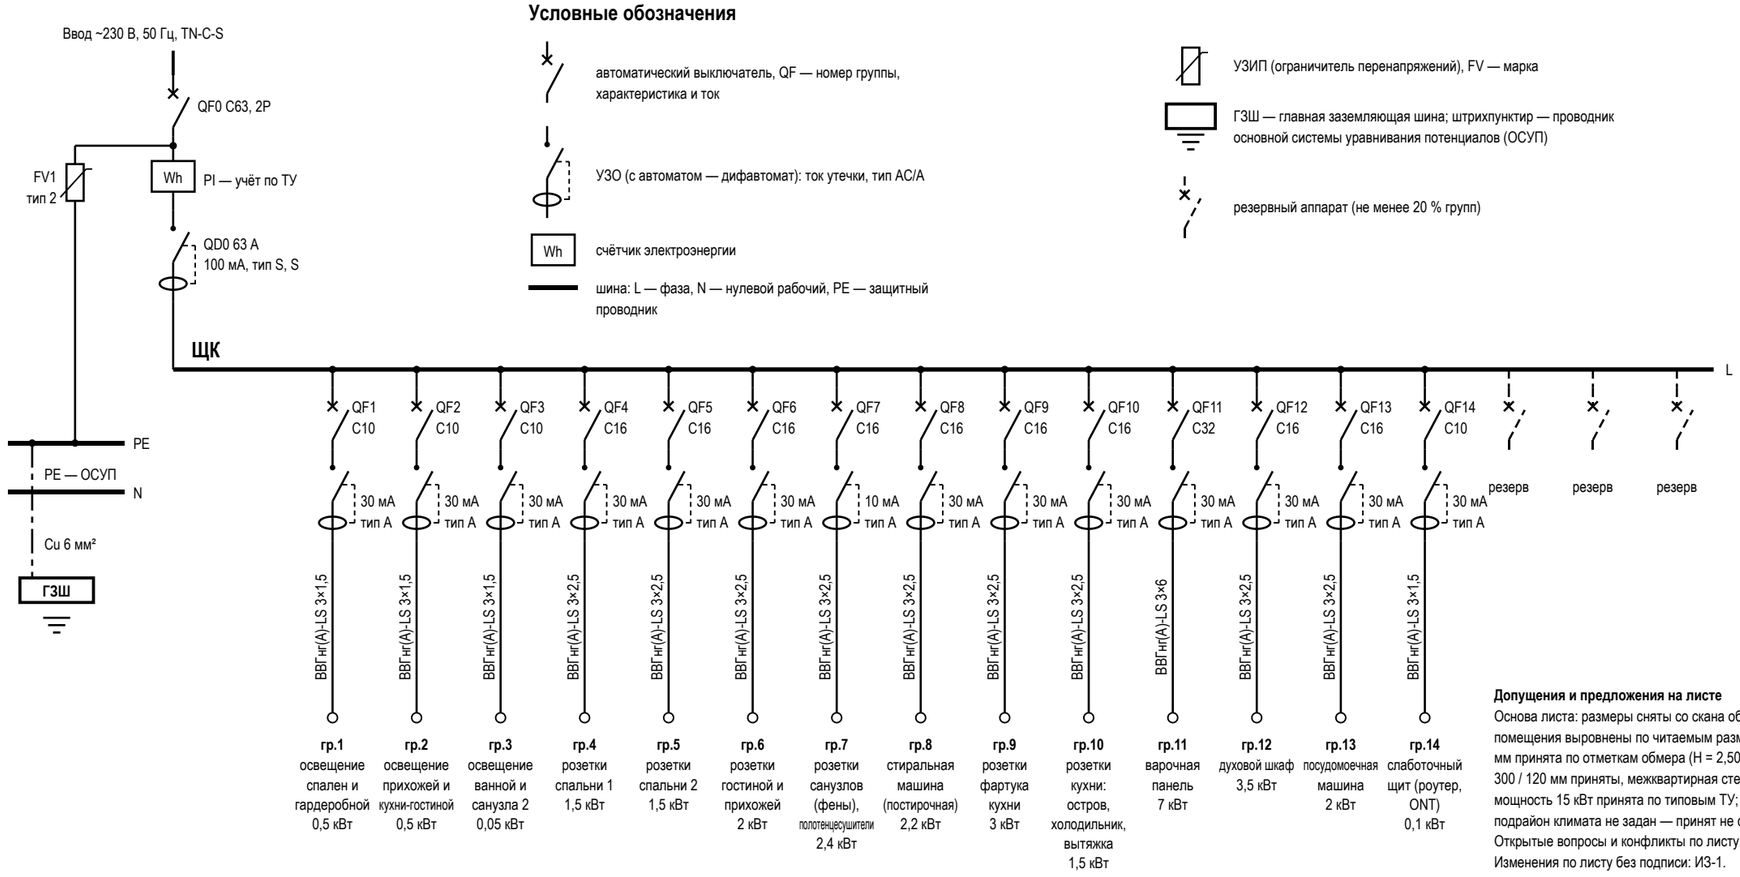


## Условные обозначения

- автоматический выключатель, QF — номер группы, характеристика и ток
- УЗО (с автоматом — дифавтомат): ток утечки, тип AC/A
- Wh — счётчик электроэнергии
- шина: L — фаза, N — нулевой рабочий, PE — защитный проводник
- УЗИП (ограничитель перенапряжений), FV — марка
- ГЗШ — главная заземляющая шина; штрихпунктир — проводник основной системы уравнивания потенциалов (ОСУП)
- резервный аппарат (не менее 20 % групп)

## Данные щитка

| Показатель | Значение |
|---|---|
| Номер щитка | ЩК |
| Тип | ЩРВ-П-24, IP41 |
| Уст. мощность, кВт | 27,75 |
| Разреш. мощность, кВт | 15 |
| Расчётная, кВт | 9,8 |
| Автоматы 1п: занят. / рез. | 14 / 3 |
| Модулей: всего / занято | 24 / 20 |
| Ток на вводе, А | 63 |
| Вводной аппарат | QF0 C63, 2P |
| УЗИП | FV1, тип 2, ЩК, после счётчика |
| ГЗШ, проводник ОСУП | Cu 6 мм² |

## Таблица групп щита ЩК и кабельный журнал

| № | Назначение | Помещения | Автомат | УЗО / дифавтомат | Кабель | Длина, м | Р, кВт | Точек |
|---|---|---|---|---|---|---|---|---|
| 1 | освещение спален и гардеробной | 1, 2, 3, 5, 7, 8, 10 | C10 | 30 мА, тип A | ВВГнг(A)-LS 3×1,5 | 173,6 | 0,5 | 63 |
| 2 | освещение прихожей и кухни-гостиной | 4, 9 | C10 | 30 мА, тип A | ВВГнг(A)-LS 3×1,5 | 41 | 0,5 | 11 |
| 3 | освещение ванной и санузла 2 | 4, 6, 10, 11 | C10 | 30 мА, тип A | ВВГнг(A)-LS 3×1,5 | 53,3 | 0,05 | 11 |
| 4 | розетки спальни 1 | 10 | C16 | 30 мА, тип A | ВВГнг(A)-LS 3×2,5 | 33 | 1,5 | 4 |
| 5 | розетки спальни 2 | 1, 3, 8 | C16 | 30 мА, тип A | ВВГнг(A)-LS 3×2,5 | 75,2 | 1,5 | 15 |
| 6 | розетки гостиной и прихожей | 4, 9 | C16 | 30 мА, тип A | ВВГнг(A)-LS 3×2,5 | 26,2 | 2 | 3 |
| 7 | розетки санузлов (фены), полотенцесушители | 6, 11 | C16 | 10 мА, тип A | ВВГнг(A)-LS 3×2,5 | 30 | 2,4 | 4 |
| 8 | стиральная машина (постирочная) | 7 | C16 | 30 мА, тип A | ВВГнг(A)-LS 3×2,5 | 20 | 2,2 | 1 |
| 9 | розетки фартука кухни | 5 | C16 | 30 мА, тип A | ВВГнг(A)-LS 3×2,5 | 16,6 | 3 | 2 |
| 10 | розетки кухни: остров, холодильник, вытяжка | 5 | C16 | 30 мА, тип A | ВВГнг(A)-LS 3×2,5 | 19 | 1,5 | 4 |
| 11 | варочная панель | 5 | C32 | 30 мА, тип A | ВВГнг(A)-LS 3×6 | 15,8 | 7 | 1 |
| 12 | духовой шкаф | 5 | C16 | 30 мА, тип A | ВВГнг(A)-LS 3×2,5 | 35,3 | 3,5 | 1 |
| 13 | посудомоечная машина | 5 | C16 | 30 мА, тип A | ВВГнг(A)-LS 3×2,5 | 53 | 2 | 1 |
| 14 | слаботочный щит (роутер, ONT) | 4 | C10 | 30 мА, тип A | ВВГнг(A)-LS 3×1,5 | 3,5 | 0,1 | 1 |
| | Итого по сечениям ВВГнг(A)-LS, м: 3×1,5 — 271,4; 3×2,5 — 308,3; 3×6 — 15,8 | | | | | 595,5 | | |

**Допущения и предложения на листе**

Основа листа: размеры сняты со скана обмерного плана KV оформление (см): часть подписей не читается, помещения выровнены по читаемым размерам; контрольный обмер не выполнен (К-1); высота потолка 2650 мм принята по отметкам обмера (H = 2,50…2,66 м, ригель 2,28 м) — уточнить при обмере (К-2); толщины стен 300 / 120 мм приняты, межквартирная стена и колонны — по скану, не замерены (К-1); разрешённая мощность 15 кВт принята по типовым ТУ; при объединении двух квартир — переоформление ТУ (К-4); подрайон климата не задан — принят не северный (жилые от 2,5 м) (К-8).
Открытые вопросы и конфликты по листу: К-4.
Изменения по листу без подписи: ИЗ-1.
См. лист открытых вопросов (лист 6, записи ИЗ-1, К-1, К-2, К-4, К-8).

## Примечания

1. Схема однолинейная: одна линия — фаза, N и PE группы; аппараты — в отключённом положении (ГОСТ 2.702, ГОСТ 2.755). Номера групп — как у точек на планах (гр.). За отметку 0,000 принят уровень чистого пола; высота щита — по плану розеток.
2. Розеточные и мокрые линии — через УЗО или дифавтомат с током утечки не более 30 мА (ПУЭ 7.1.79); в санузле выполнить ДСУП (ПУЭ 7.1.87–7.1.88).
3. УЗО тип A — для линий с электроникой, стиральной и посудомоечной машиной, LED-драйверами; тип AC — только для чисто активной нагрузки.
4. Кабель — медный, исполнение нг(A)-LS (ГОСТ 31565-2012); скрытая прокладка только горизонтально и вертикально, фактические трассы зафиксировать исполнительной схемой до закрытия отделкой.
5. Номинал автомата — не выше допустимого тока кабеля: 1,5 мм² — до 10 А, 2,5 мм² — до 16 А. Резерв щита — не менее 20 % модулей.
6. Расчёт нагрузок, токов КЗ, селективности и сечений — по проекту ЭОМ организации с допуском СРО; лист задаёт состав, расположение и группы.
7. УЗИП FV1 — после вводного автомата, проводник к шине PE — кратчайший, без петель. Шина PE щита соединяется с ГЗШ проводником ОСУП; к ГЗШ присоединяются трубы водопровода и отопления на вводе в квартиру (ПУЭ 7.1.87). Шины N и PE — раздельные, после разделения PEN не объединяются.
8. До подключения нагрузки — приёмо-сдаточные испытания с протоколом: сопротивление изоляции линий не менее 0,5 МОм, срабатывание УЗО по току и времени, непрерывность защитных проводников PE (ПУЭ, гл. 1.8).

| Изм. | Кол.уч | Лист | № док. | Подп. | Дата |
|---|---|---|---|---|---|
| Разраб. | | Кырлан А.С. | | | 04.11.26 |
| Пров. | | | | | |
| ГИП | | | | | |
| | | | | | |
| Н. контр. | | | | | |
| Утв. | | | | | |

**ГД-2026-009-АИ**

Квартира 103 м²

Общая площадь 100,72* м² · * размеры со скана, не замерены (реестр — л. 6, 7, К-1)

Дизайн-проект интерьера

| Стадия | Лист | Листов |
|---|---|---|
| РП | 28 | 120 |

**Однолинейная схема щита**


М б/м

**Кырлан Александр Сергеевич**

# План принципиальных трасс

Силовые трассы и объёмы электромонтажа, слаботочка в объёмах · размеры в мм



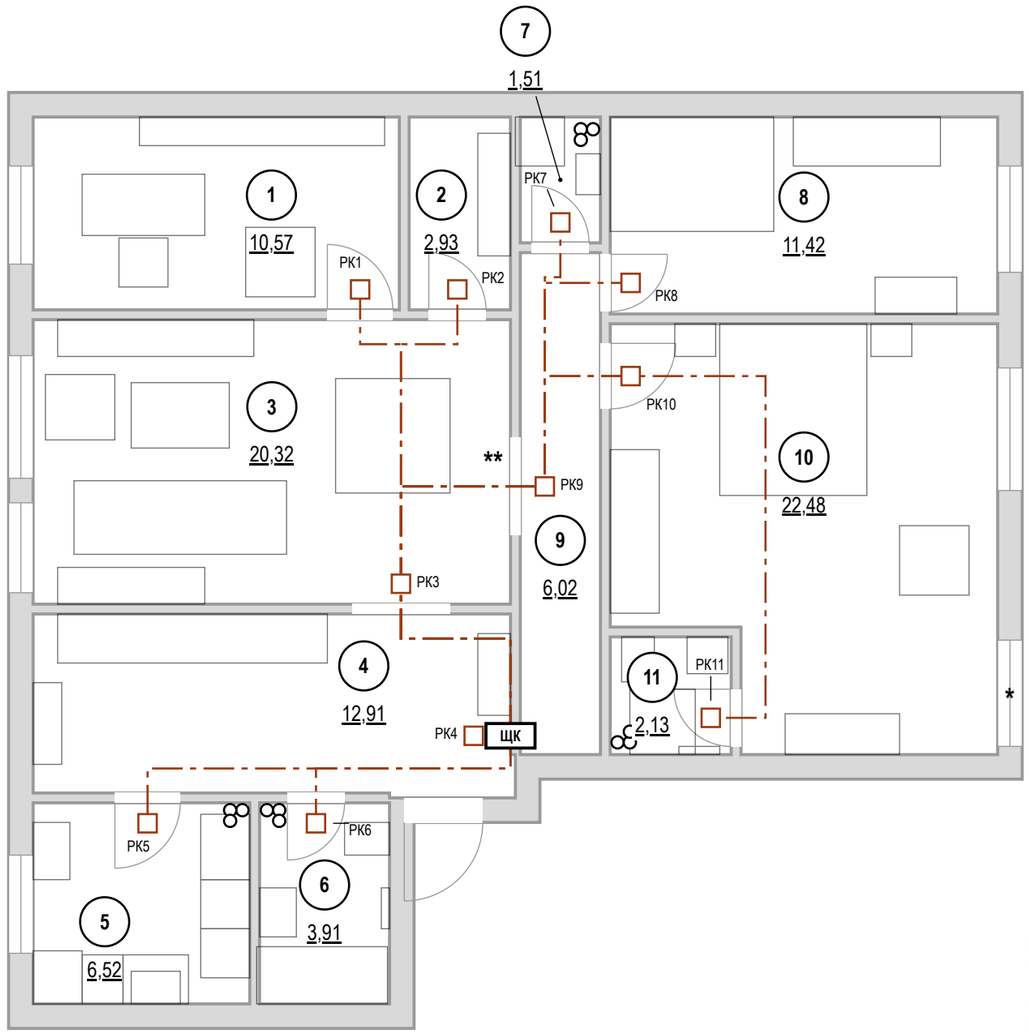


## Кабель по группам ВВГнг(А)-LS, м

| Гр. | мм² | Трасса | Данные |
|---|---|---|---|
| 1 | 3×1,5 | 175,3 | 173,6 |
| 2 | 3×1,5 | 40,9 | 41 |
| 3 | 3×1,5 | 55,1 | 53,3 |
| 4 | 3×2,5 | 33 | 33 |
| 5 | 3×2,5 | 75,2 | 75,2 |
| 6 | 3×2,5 | 26,2 | 26,2 |
| 7 | 3×2,5 | 40,6 | 30 |

| Гр. | мм² | Трасса | Данные |
|---|---|---|---|
| 8 | 3×2,5 | 17,9 | 20 |
| 9 | 3×2,5 | 16,6 | 16,6 |
| 10 | 3×2,5 | 19 | 19 |
| 11 | 3×6 | 15,8 | 15,8 |
| 12 | 3×2,5 | 15,4 | 35,3 |
| 13 | 3×2,5 | 13,4 | 53 |
| 14 | 3×1,5 | 3,5 | 3,5 |
| **Σ** | | **547,9** | **595,5** |

## Объёмы прокладки

| Работа, материал | Ед. | Кол. |
|---|---|---|
| Гофротруба Ø20 в потолочном пространстве | м | 251,6 |
| Кабель-канал плинтуса для силовых линий | м | 129,5 |
| Короб или накладной канал для вертикальных спусков и подъёмов | м | 83,8 |
| Коробка распределительная (РК) над дверью помещения | шт | 11 |
| Слаботочка: кабель домофона | м | 4,3 |
| Слаботочка: Кабель коаксиальный RG-6 (75 Ом) к розеткам ТВ | м | 16,1 |
| Слаботочка: U/UTP кат. 6 (LAN, Wi-Fi, камеры) | м | 70,3 |
| Слаботочка: гофротруба Ø20 отдельно от силовых | м | 81,6 |

## Экспликация помещений

| № | Помещение | Площадь, м² |
|---|---|---|
| 1 | Кабинет-библиотека | 10,57 |
| 2 | Кладовая | 2,93 |
| 3 | Гостиная-столовая | 20,32 |
| 4 | Прихожая-холл | 12,91 |
| 5 | Кухня | 6,52 |
| 6 | Ванная | 3,91 |
| 7 | Постирочная | 1,51 |
| 8 | Спальня 2 | 11,42 |
| 9 | Коридор | 6,02 |
| 10 | Спальня мастер | 22,48 |
| 11 | Ванная мастер | 2,13 |
| | Итого (общая площадь) | 100,72 |

## Штробы — только после заключения

| Работа | Ед. | Кол. |
|---|---|---|
| Вертикальные штробы 20×20 мм от потолка до каждой настенной точки (в маршрут без штроб не входят) | м | 103,59 |

## Условные обозначения

- **ЩК** — щит квартирный
- РК — распределительная коробка над дверью помещения
- магистраль от щита к РК: потолочное пространство, гофра
- мебель и сантехприборы — подложка

Допущения и предложения на листе. Основа листа: размеры сняты со скана обмерного плана KV оформление (см): часть подписей не читается, помещения выровнены по читаемым размерам; контрольный обмер не выполнен (К-1); высота потолка 2650 мм принята по отметкам обмера (Н = 2,50…2,66 м, ригель 2,28 м) — уточнить при обмере (К-2); толщины стен 300 / 120 мм приняты, межквартирная стена и колонны — по скану, не замерены (К-1); разрешённая мощность 15 кВт принята по типовым ТУ; при объединении двух квартир — переоформление ТУ (К-4); подрайон климата не задан — принят не северный (жилые от 2,5 м) (К-8). Знак «*» — принято, не замерено и не подтверждено (замерить на объекте): К-6: Ст К1-3, Ст В1-3, Ст Т3-3 — положение снято со скана обмера, отдельно не замерялось; ось внутри габарита поддона См1 — обмер угла по К-6. Знак «**» — предложение проектировщика, заказчиком не утверждено (согласовать с заказчиком): ЩС — щит слаботочный: место и состав. См. лист открытых вопросов (лист 6, записи К-1, К-2, К-4–К-6, К-8).

## Примечания

1. За отметку 0,000 принят уровень чистого пола. Высоты Н — от чистого пола до оси изделия; привязки — от чистовой грани стены до оси механизма (у рамки на несколько постов — до оси рамки).
2. Розеточные и мокрые линии — через УЗО или дифавтомат с током утечки не более 30 мА (ПУЭ 7.1.79); в санузле выполнить ДСУП (ПУЭ 7.1.87–7.1.88).
3. Кабель — медный, исполнение нг(А)-LS (ГОСТ 31565-2012); скрытая прокладка только горизонтально и вертикально, фактические трассы зафиксировать исполнительной схемой до закрытия отделкой.
4. Расчёт нагрузок, токов КЗ, селективности и сечений — по проекту ЭОМ организации с допуском СРО; лист задаёт состав, расположение и группы.
5. Длины — по плану: от щита вверх в потолочное пространство, по дверям и коридору без захода в мокрые помещения к распределительной коробке над дверью, далее к точкам; вертикали считаются вниз и обратно (у последней точки цепочки — в один конец); запас 10 %. Трассы принципиальные: фактическую зафиксировать исполнительной схемой до закрытия отделкой.
6. Несущие стены не определены: штробы в стенах не выполнять. Маршрут проложен без штроб: горизонтали — за потолком в гофре (251,6 м) и в кабель-канале плинтуса (129,5 м), вертикали — в коробе или накладном канале (147,4 м кабеля). Точек: за потолком — 59, спуск из потолка — 13, по плинтусу — 19, плинтус и подъём 31.
7. Вариант со штробами — работа после технического заключения: 103,59 м вертикальных штроб от потолка до каждой настенной точки; условие — только после технического заключения: стена не несущая (или вертикальная штроба в несущей согласована конструктором), глубина и ширина 20–25 мм, не в зонах 0–2 ванной. Без заключения и согласования конструктора в смету и в график эта работа не входит.
8. В данных проекта (журнал щита) длины кабеля внесены оценкой (596 м), по трассам из геометрии — 548 м (-8 %): к закупке и в смету принимать длины по трассам, а оценку в данных проекта заменить.
9. Слаботочные сети: кабели и точки считаются по лучам от ЩС** (лист слаботочных сетей): 91 м, портов патч-панели и коммутатора не менее 5; из точек 2 предложения листа слаботочки, не подтверждённые заказчиком. Изделия — в ведомости изделий.

1000 мм · печать 1:1

| Изм. | Кол.уч | Лист | № док. | Подп. | Дата |
|---|---|---|---|---|---|
| Разраб. | | Кырлан А.С. | | | 04.11.26 |
| Пров. | | | | | |
| ГИП | | | | | |
| | | | | | |
| Н. контр. | | | | | |
| Утв. | | | | | |

**ГД-2026-009-АИ**

Квартира 103 м²

Общая площадь 100,72* м² · * размеры со скана, не замерены (реестр — л. 6, 7, К-1)

Дизайн-проект интерьера

| Стадия | Лист | Листов |
|---|---|---|
| РП | 29 | 120 |

**План принципиальных трасс**

М 1:75


**Кырлан Александр Сергеевич**

выпуск 04.11.2026 № 35b47f1c2a · стр. 32 из 130

# План слаботочных сетей

Интернет, ТВ, домофон · размеры в мм · высоты от чистого пола

**ПРЕДВАРИТЕЛЬНО · не для производства работ · открыто пунктов: 8 (реестр — л. 6, 7)**

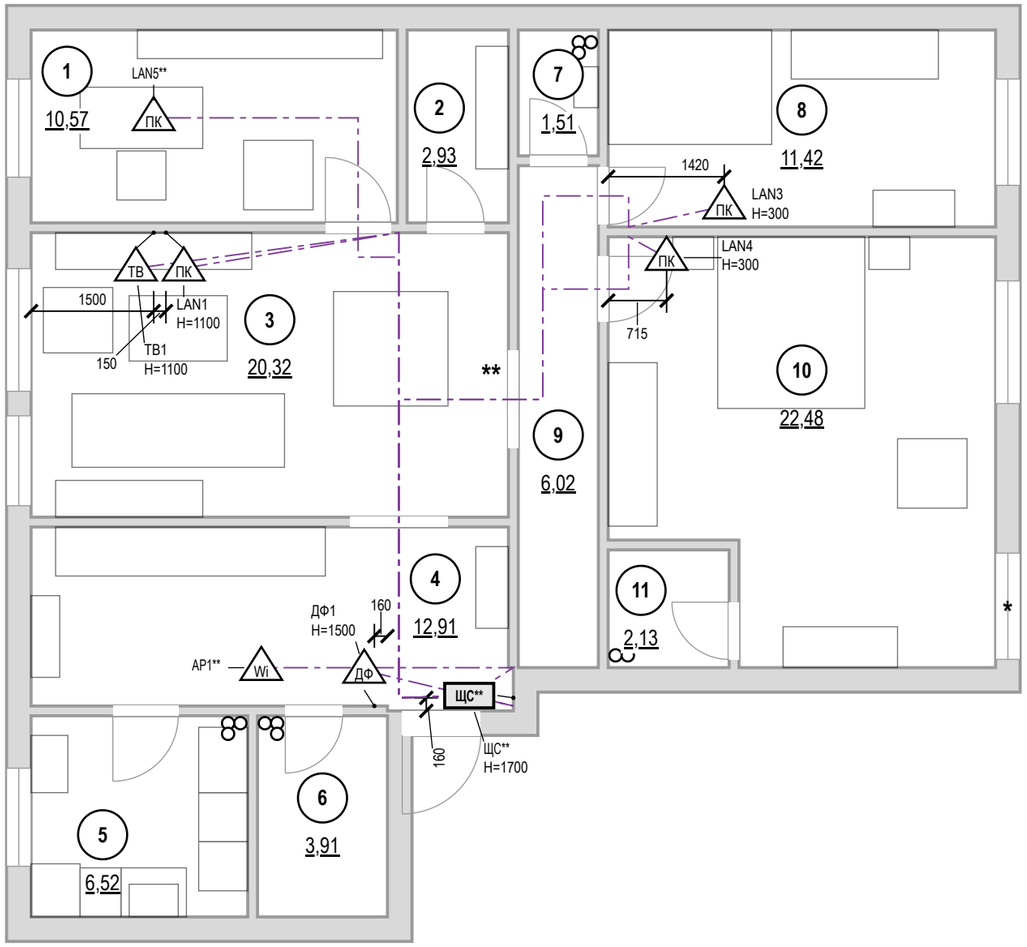


## Ведомость слаботочных точек

| Марка | Пом. | Назначение | H, мм | Кабель |
|---|---|---|---|---|
| LAN5** | 1 | розетка LAN (RJ45) | 0 | U/UTP кат. 6 |
| ТВ1 | 3 | розетка ТВ | 1100 | коаксиальный RG-6 |
| LAN1 | 3 | розетка LAN (RJ45) | 1100 | U/UTP кат. 6 |
| ЩС** | 4 | щит слаботочный | 1700 | ввод пров. |
| ДФ1 | 4 | домофон (трубка) | 1500 | по системе |
| AP1** | 4 | точка доступа Wi-Fi | | U/UTP кат. 6 |
| LAN3 | 8 | розетка LAN (RJ45) | 300 | U/UTP кат. 6 |
| LAN4 | 10 | розетка LAN (RJ45) | 300 | U/UTP кат. 6 |

## Условные обозначения

- **ЩС** — щит слаботочный: ввод провайдера, роутер, коммутатор
- ПК — розетка компьютерная RJ45
- ТВ — розетка телевизионная
- ДФ — трубка или монитор домофона
- Wi — точка доступа Wi-Fi (питание PoE)
- кабель от ЩС до точки, отдельным лучом
- мебель и сантехприборы — подложка
- стояк: К1 — канализация, В1 — ХВС, Т3 — ГВС
- 1 — номер помещения, площадь м²

**Допущения и предложения на листе**

Основа листа: размеры сняты со скана обмерного плана KV оформление (см): часть подписей не читается, помещения выровнены по читаемым размерам; контрольный обмер не выполнен (К-1); высота потолка 2650 мм принята по отметкам обмера (Н = 2,50…2,66 м, ригель 2,28 м) — уточнить при обмере (К-2); толщины стен 300 / 120 мм приняты, межквартирная стена и колонны — по скану, не замерены (К-1); разрешённая мощность 15 кВт принята по типовым ТУ; при объединении двух квартир — переоформление ТУ (К-4); подрайон климата не задан — принят не северный (жилые от 2,5 м) (К-8).

Знак «*» — принято, не замерено и не подтверждено (замерить на объекте): К-1: окно пом. 10 (стена Б) — Окно 1300 при смещение 3500 на стене Б основной части (длина 3830) выходило за стену на 970 мм; К-6: Ст К1-3, Ст В1-3, Ст Т3-3 — положение снято со скана обмера, отдельно не замерялось; ось внутри габарита поддона См1 — обмер угла по К-6.

Знак «**» — предложение проектировщика, заказчиком не утверждено (согласовать с заказчиком): LAN5 — стол Б2 стоит посреди помещения — питание из лючка в полу под столом: трасса в конструкции пола (толщина стяжки — по обмеру) — согласовать с заказчиком; ЩС — щит слаботочный: место и состав; AP1 — точка доступа Wi-Fi: число и места; К-5: дверь пом. 3 (стена Б) — проём в межквартирной стене — объединение квартир, предложение до техзаключения.

См. лист открытых вопросов (лист 6, записи К-1, К-2, К-4–К-6, К-8).

## Примечания

1. За отметку 0,000 принят уровень чистого пола. Высоты Н — от чистого пола до оси изделия; привязки — от чистовой грани стены до оси механизма (у рамки на несколько постов — до оси рамки).
2. Высота установки, не указанная на плане: розетки LAN и ТВ — 300 мм от чистого пола.
3. Слаботочные кабели — отдельно от силовых: в своей трубе или лотке, при параллельной прокладке не ближе 100 мм к силовым, пересечения под прямым углом; каждую точку — отдельным кабелем от ЩС** без скруток.
4. Трассы на листе — принципиальные; фактические зафиксировать исполнительной схемой до закрытия отделкой. Силовые линии, УЗО 30 мА, ДСУП, кабель нг(А)-LS — по листам розеток и щита.
5. Проект силовой части и расчёт токов КЗ — по проекту ЭОМ; слаботочная часть согласуется с провайдером и управляющей компанией (домофон, коллективное ТВ).

1000 мм · печать 1:1

| Изм. | Кол.уч | Лист | № док. | Подп. | Дата |
|---|---|---|---|---|---|
| Разраб. | | Кырлан А.С. | | | 04.11.26 |
| Пров. | | | | | |
| ГИП | | | | | |
| | | | | | |
| Н. контр. | | | | | |
| Утв. | | | | | |

**ГД-2026-009-АИ**

Квартира 103 м²

Общая площадь 100,72* м² · * размеры со скана, не замерены (реестр — л. 6, 7, К-1)

Дизайн-проект интерьера

| Стадия | Лист | Листов |
|---|---|---|
| РП | 30 | 120 |

**План слаботочных сетей**

М 1:75

**Кырлан Александр Сергеевич**

выпуск 04.11.2026 № 35b47f1c2a · стр. 33 из 130

04

# Отопление и вентиляция


Кырлан Александр Сергеевич

выпуск 04.11.2026 · 35b47f1c2a · стр. 34 из 130

# План вентиляции

Вытяжка, приток, переток · кондиционирование не предусмотрено · размеры в мм · высоты от чистого пола

**ПРЕДВАРИТЕЛЬНО · не для производства работ · открыто пунктов: 8 (реестр — л. 6, 7)**

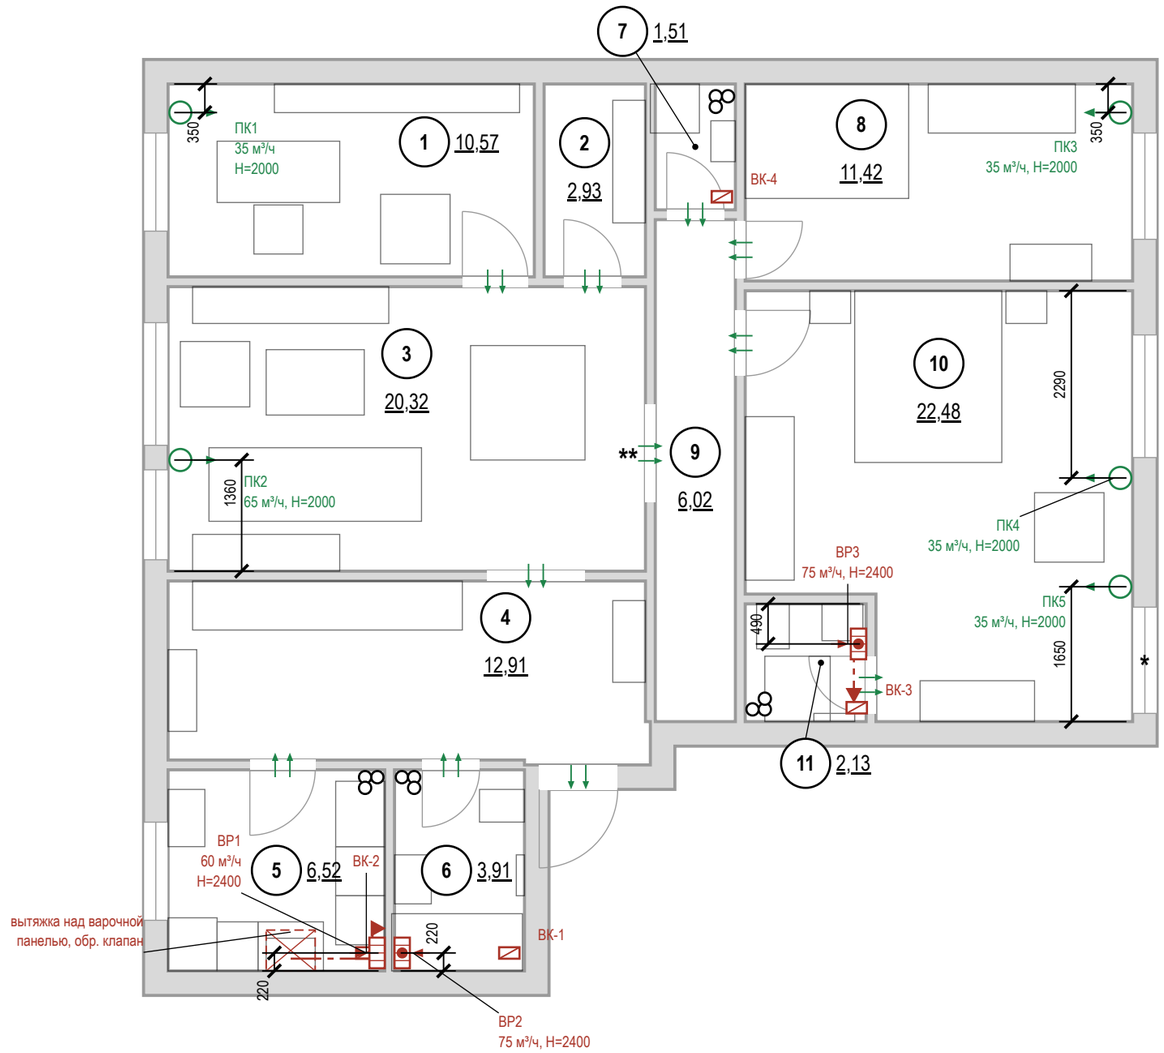


## Условные обозначения

- стояк: К1 — канализация, В1 — ХВС, Т3 — ГВС
- 1 — номер помещения, площадь м²
- вытяжная решётка в вентканал: марка, расход м³/ч, H центра от чистого пола
- вытяжная решётка с бытовым вентилятором и обратным клапаном: марка, расход, H
- приточный клапан (КИВ) в наружной стене: марка, расход, H центра
- переток: зазор под полотном или переточная решётка
- кухонная вытяжка над варочной панелью
- ВК-N — вентканал в стене или вентблоке
- воздуховод в коробе под потолком (за подшивным потолком) до вентканала
- отдельный вход воздуховода в вентканал, обратный клапан
- * — «*» — принято, не замерено и не подтверждено
- ** — «**» — предложение проектировщика, заказчиком не утверждено

## Воздухообмен, м³/ч

| № | Помещение | Выт. норма | Выт. проект | Прит. норма | Прит. проект | Устрой-ства |
|---|---|---|---|---|---|---|
| 1 | Кабинет-библиотека | | | 32 | 35 | ПК1 |
| 2 | Кладовая | 2 | | | | переток |
| 3 | Гостиная-столовая | | | 61 | 65 | ПК2 |
| 5 | Кухня | 60 | 60 | | | ВР1 |
| 6 | Ванная | 50 | 75 | | | ВР2 |
| 7 | Постирочная | 1 | | | | переток |
| 8 | Спальня 2 | | | 35 | 35 | ПК3 |
| 10 | Спальня мастер | | | 68 | 70 | ПК4, ПК5 |
| 11 | Ванная мастер | 50 | 75 | | | ВР3 |
| | **Итого** | **163** | **210** | **196** | **205** | |
| | Норма по жильцам: 30×2 | | | 60 | | |

Воздухообмен квартиры — по большей из сумм притока и вытяжки: норма 196 м³/ч, проект 210 м³/ч.
Вытяжка не меньше притока — баланс сведён.

**Допущения и предложения на листе**

Основа листа: размеры сняты со скана обмерного плана KV оформление (см): часть подписей не читается, помещения выровнены по читаемым размерам; контрольный обмер не выполнен (К-1); высота потолка 2650 мм принята по отметкам обмера (H = 2,50…2,66 м, ригель 2,28 м) — уточнить при обмере (К-2); толщины стен 300 / 120 мм приняты, межквартирная стена и колонны — по скану, не замерены (К-1); разрешённая мощность 15 кВт принята по типовым ТУ; при объединении двух квартир — переоформление ТУ (К-4); подрайон климата не задан — принят не северный (жилые от 2,5 м) (К-8).
Знак «*» — принято, не замерено и не подтверждено (замерить на объекте): К-1: окно пом. 10 (стена Б) — Окно 1300 при смещение 3500 на стене Б основной части (длина 3830) выходило за стену на 970 мм; К-6: Ст К1-3, Ст В1-3, Ст Т3-3 — положение снято со скана обмера, отдельно не замерялось; ось внутри габарита поддона См1 — обмер угла по К-6.
Знак «**» — предложение проектировщика, заказчиком не утверждено (согласовать с заказчиком): К-5: дверь пом. 3 (стена Б) — проём в межквартирной стене — объединение квартир, предложение до техзаключения.
См. лист открытых вопросов (лист 6, записи К-1, К-2, К-4–К-6, К-8).

## Примечания

1. Расчёт систем ОВ и подбор оборудования — проектная организация с допуском СРО; лист даёт места, трассы и привязки.
2. Нормы вытяжки — СП 54.13330.2022 (Изм. 1, 2), табл. 7.1: кухня с электроплитой 60 м³/ч, с газовой 100; ванная и совмещённый санузел 50; уборная 25; гардеробная 0,2 ч⁻¹. Приток в жилые — 3 м³/ч на 1 м² (менее 20 м² общей площади на человека), иначе 30 м³/ч на человека.
3. Вентканалы и шахты не сужать, не переносить и не закрывать; вентилятор и кухонная вытяжка — через обратный клапан, без перекрытия естественной тяги; ВР3 — воздуховодом до ВК-3 ≈ 0,9 м в коробе под потолком.
4. Проектные расходы — не ниже нормы, вытяжка сведена с притоком вентиляторами мокрых помещений. Клапаны — в простенке у окна, центр 2000 мм, не над кроватью, не ближе 300 мм к стоякам отопления; типоразмер — на расход.
5. Кухонная вытяжка в воздухообмен не включена: воздуховод не менее Ø125 в коробе, вход в канал отдельный.
6. Переток — зазор под полотнами межкомнатных дверей или переточная решётка.
7. Кондиционирование заданием не предусмотрено; при установке трассы фреона и дренажа (не менее 40 мм/м, в К1 через сифон) и питание заложить до черновых работ.
8. Привязки оборудования — по паспортам приобретённых моделей, до черновых работ.
9. Знак «*» у проёма — допущение: положение проёма не замерено (окно пом. 10, стена Б); размер напечатан как принятый. Реестр: листы 6–7, вопрос К-1.
10. Клапаны ПК4, ПК5 выведены в простенок у окна, положение которого — допущение (знак «*»): после обмера окна привязку сверить.

1000 мм · печать 1:1

| Изм. | Кол.уч | Лист | № док. | Подп. | Дата |
|---|---|---|---|---|---|
| Разраб. | | Кырлан А.С. | | | 04.11.26 |
| Пров. | | | | | |
| ГИП | | | | | |
| | | | | | |
| Н. контр. | | | | | |
| Утв. | | | | | |

**ГД-2026-009-АИ**

Квартира 103 м²

Общая площадь 100,72* м² · * размеры со скана, не замерены (реестр — л. 6, 7, К-1)

Дизайн-проект интерьера

| Стадия | Лист | Листов |
|---|---|---|
| РП | 31 | 120 |

**План вентиляции**

М 1:75


**Кырлан Александр Сергеевич**

выпуск 04.11.2026 № 35b47f1c2a · стр. 35 из 130

# План отопления

Радиаторы, стояки, подводки · размеры в мм · высоты от чистого пола

**ПРЕДВАРИТЕЛЬНО · не для производства работ · открыто пунктов: 8 (реестр — л. 6, 7)**

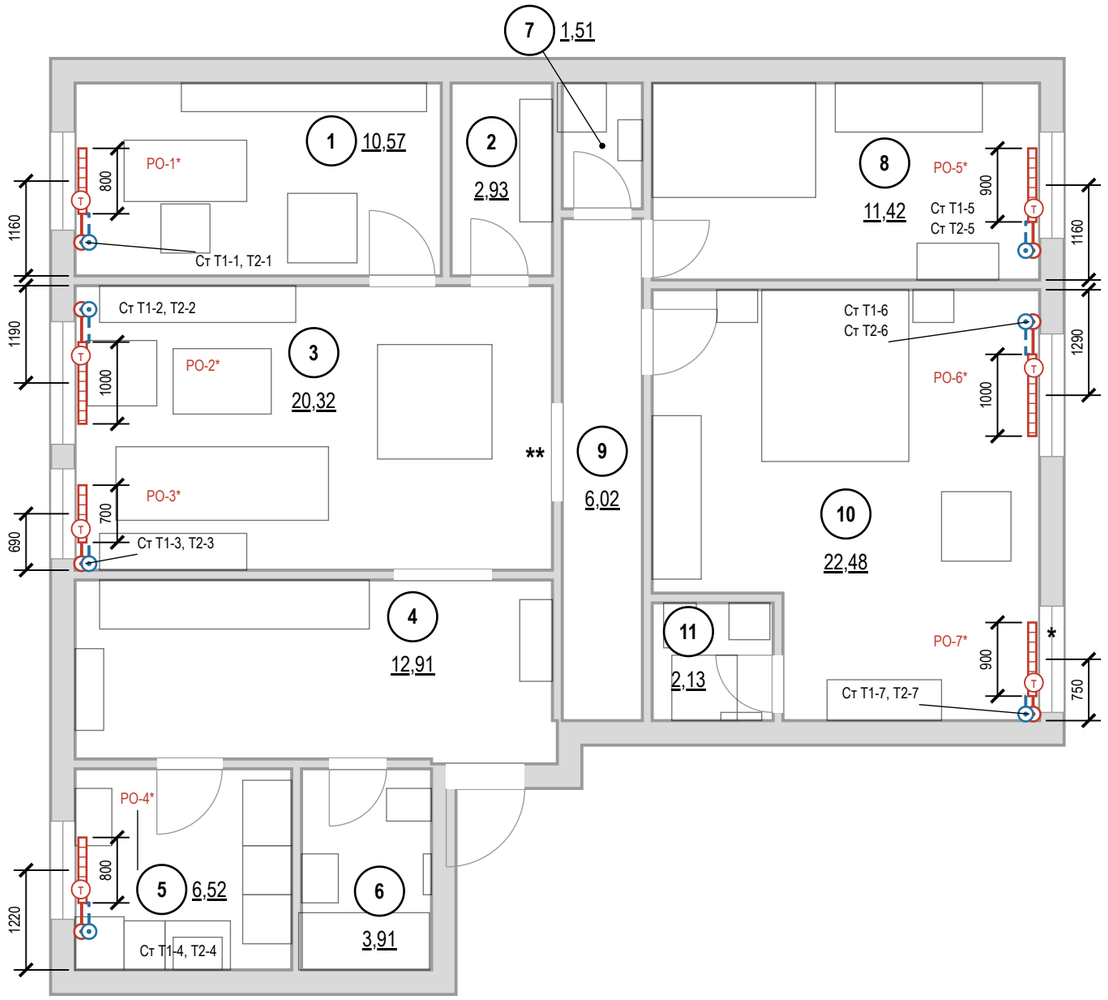


## Условные обозначения

- (1) — номер помещения, площадь м²
- радиатор отопления (марка РО-N, длина по плану)
- (Т) — клапан с термоголовкой на подаче
- стояк отопления, подающий (Ст Т1-N)
- стояк отопления, обратный (Ст Т2-N)
- Т1 — отопление, подающий трубопровод
- Т2 — отопление, обратный трубопровод
- * — «*» — принято, не замерено и не подтверждено
- ** — «**» — предложение проектировщика, заказчиком не утверждено

## Ведомость радиаторов

| Марка | Помещение | Тип | Д×В×Г, мм | Низ / стена | Q, Вт |
|---|---|---|---|---|---|
| РО-1 | 1. Кабинет-библиотека | панельный* | 800×400×100 | 120 / 40 | расч. |
| РО-2 | 3. Гостиная-столовая | панельный* | 1000×400×100 | 120 / 40 | расч. |
| РО-3 | 3. Гостиная-столовая | панельный* | 700×400×100 | 120 / 40 | расч. |
| РО-4 | 5. Кухня | панельный* | 800×500×100 | 120 / 40 | расч. |
| РО-5 | 8. Спальня 2 | панельный* | 900×500×100 | 120 / 40 | расч. |
| РО-6 | 10. Спальня мастер | панельный* | 1000×500×100 | 120 / 40 | расч. |
| РО-7 | 10. Спальня мастер | панельный* | 900×500×100 | 120 / 40 | расч. |

* тип и мощность — по теплотехническому расчёту
Низ — от чистого пола, стена — зазор до задней панели, мм.

**Привязки — до обмера**
Стояки отопления в исходных данных не заданы: показаны у откосов окон, подводки — принципиально. До черновых работ — обмер стояков и паспорта приборов; лист перевыпустить по факту.

## Примечания

1. Расчёт системы отопления, теплопотерь и подбор приборов — проектная организация с допуском СРО; лист даёт места и привязки.
2. Тип, длина и мощность радиаторов — по теплотехническому расчёту; лист задаёт места, зазоры и подключение.
3. Радиаторы — под каждым окном жилых комнат и кухни, центр по оси проёма, длина 0,7 ширины окна (кратно 100); окончательно — по расчёту.
4. Зазоры радиатора: низ не менее 100 мм от чистого пола, верх не менее 100 мм до подоконника, 30–50 мм от стены до задней панели; центр по оси окна с допуском ±20 мм. Верх до подоконника — 215 мм (РО-1 — 200, РО-4 — 143, РО-5 — 163, РО-6 — 205, РО-7 — 205).
5. Радиаторы не закрывать глухими коробами и мебелью; перенос и замена приборов в многоквартирном доме — переустройство, согласование с управляющей организацией (ЖК РФ ст. 25–26); вынос на лоджию запрещён.
6. Трубы отопления через межквартирные стены не прокладывать (СП 51.13330.2011, п. 9.19); через перекрытия и перегородки — в гильзах.
7. Привязки приборов и подводок — по паспортам приобретённых радиаторов и клапанов, до черновых работ.
8. До закрытия отделкой трубопроводы отопления испытать гидростатическим давлением с оформлением акта (СП 73.13330.2016, 7.2–7.3).
9. Знак «*» у проёма — допущение: положение проёма не замерено (окно пом. 10, стена Б); размер напечатан как принятый. Реестр: листы 6–7, вопрос К-1.
10. Радиатор РО-7 стоит по оси окна, положение которого — допущение (знак «*»): после обмера окна привязки прибора и подводок сверить.

Допущения и предложения на листе. Основа листа: размеры сняты со скана обмерного плана KV оформление (см): часть подписей не читается, помещения выровнены по читаемым размерам; контрольный обмер не выполнен (К-1); высота потолка 2650 мм принята по отметкам обмера (Н = 2,50…2,66 м, ригель 2,28 м) — уточнить при обмере (К-2); толщины стен 300 / 120 мм приняты, межквартирная стена и колонны — по скану, не замерены (К-1); разрешённая мощность 15 кВт принята по типовым ТУ; при объединении двух квартир — переоформление ТУ (К-4); подрайон климата не задан — принят не северный (жилые от 2,5 м) (К-8). Знак «*» — принято, не замерено и не подтверждено (замерить на объекте). Знак «**» — предложение проектировщика, заказчиком не утверждено (согласовать с заказчиком). См. лист открытых вопросов (лист 6, записи К-1, К-2, К-4, К-5, К-8).

1000 мм · печать 1:1

| Изм. | Кол.уч | Лист | № док. | Подп. | Дата |
|---|---|---|---|---|---|
| Разраб. | | Кырлан А.С. | | | 04.11.26 |
| Пров. | | | | | |
| ГИП | | | | | |
| Н. контр. | | | | | |
| Утв. | | | | | |

**ГД-2026-009-АИ**

Квартира 103 м²

Общая площадь 100,72* м² · * размеры со скана, не замерены (реестр — л. 6, 7, К-1)

Дизайн-проект интерьера

| Стадия | Лист | Листов |
|---|---|---|
| РП | 32 | 120 |

**План отопления**

М 1:75

**Кырлан Александр Сергеевич**

выпуск 04.11.2026 № 35b47f1c2a · стр. 36 из 130

05

# Водоснабжение и канализация

Кырлан Александр Сергеевич


выпуск 04.11.2026 № 35b47f1c2a · стр. 37 из 130

# План выводов сантехники


Выводы В1, Т3, К1 · привязки от чистовых стен · высоты от чистого пола, мм

**ПРЕДВАРИТЕЛЬНО · не для производства работ · открыто пунктов: 8 (реестр — л. 6, 7)**


### Фрагмент 1. Ванная (пом. 6)

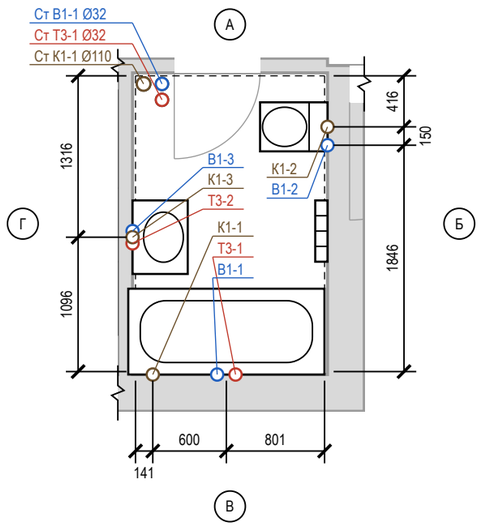



### Фрагмент 2. Постирочная (пом. 7)

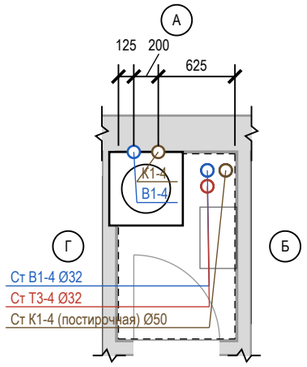


### Фрагмент 3. Ванная мастер (пом. 11)

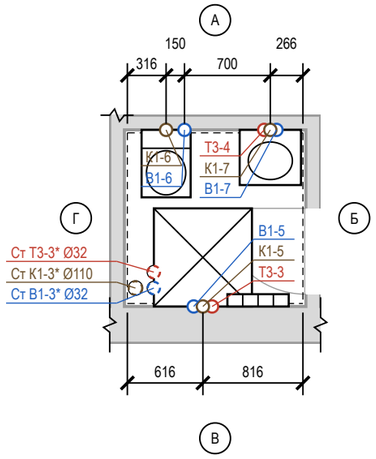


### Фрагмент 4. Кухня (пом. 5)

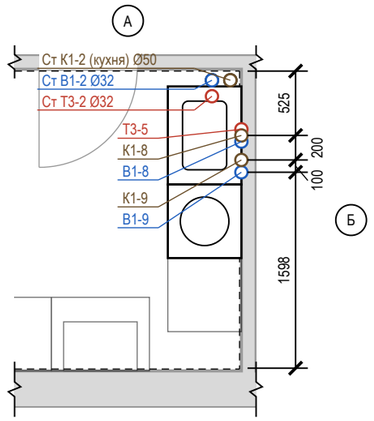


## Ведомость привязок выводов

| Код | Прибор | Ø | Н, мм | Привязка от чист. стен, мм | Прим. |
|---|---|---|---|---|---|
| В1-1 | См1 ванна | ½" | 800* | ст. В: 666 от Г | межос. 150 |
| Т3-1 | См1 ванна | ½" | 800* | ст. В: 726 от Б | межос. 150 |
| К1-1 | См1 ванна | Ø50 | 50* | ст. В: 141 от Г | |
| В1-2 | См2 унитаз подвесной | ½" | 250* | ст. Б: 566 от А | в раме инсталляции |
| К1-2 | См2 унитаз подвесной | Ø110 | 220* | ст. Б: 416 от А | |
| В1-3 | См3 умывальник | ½" | 600* | ст. Г: 1146 от В | межос. 100 |
| Т3-2 | См3 умывальник | ½" | 600* | ст. Г: 1046 от В | межос. 100 |
| К1-3 | См3 умывальник | Ø50 | 500* | ст. Г: 1096 от В | |
| В1-4 | Пм1 стиральная машина | ½" | 600* | ст. А: 125 от Г | кран машины |
| К1-4 | Пм1 стиральная машина | Ø50 | 600* | ст. А: 325 от Г | |
| В1-5 | См1 душ | ½" | 1200* | ст. В: 541 от Г | межос. 150 |
| Т3-3 | См1 душ | ½" | 1200* | ст. В: 691 от Г | межос. 150 |
| К1-5 | См1 душ | Ø50 | 70* | ст. В: 616 от Г | сифон поддона |
| В1-6 | См2 унитаз подвесной | ½" | 250* | ст. А: 466 от Г | в раме инсталляции |
| К1-6 | См2 унитаз подвесной | Ø110 | 220* | ст. А: 316 от Г | |
| В1-7 | См3 умывальник | ½" | 600* | ст. А: 216 от Б | межос. 100 |
| Т3-4 | См3 умывальник | ½" | 600* | ст. А: 316 от Б | межос. 100 |
| К1-7 | См3 умывальник | Ø50 | 500* | ст. А: 266 от Б | |
| В1-8 | Кх1 мойка кухонная | ½" | 600* | ст. Б: 575 от А | межос. 100 |
| Т3-5 | Кх1 мойка кухонная | ½" | 600* | ст. Б: 475 от А | межос. 100 |
| К1-8 | Кх1 мойка кухонная | Ø50 | 400* | ст. Б: 525 от А | |
| В1-9 | Кх2 посудомоечная машина | ½" | 550* | ст. Б: 825 от А | кран ПММ в шкафу мойки |
| К1-9 | Кх2 посудомоечная машина | Ø40 | 550* | ст. Б: 725 от А | слив ПММ в шкафу мойки |

* — высота по практике монтажа; сверить по паспорту прибора

## Условные обозначения

- вывод В1 (код — в ведомости привязок)
- вывод Т3 (код — в ведомости привязок)
- вывод К1 (код — в ведомости привязок)
- сантехприбор по расстановке (габарит модели)
- чистовая поверхность стены (от неё привязки)
- стояк «Ст К1-N / Ст В1-N» (ГОСТ 21.601), Ø мм
- * стояк Т3 не на обмере — принят в шахте рядом со Ст В1, сверить
- * у стояка — положение принято, не замерено, сверить
- линия обрыва (граница фрагмента)
- А обозначение стены А–Г (как на развёртках)

## Примечания

1. Привязки выводов даны от чистовых поверхностей стен (облицовка на сторону: ванная — 24 мм (штукатурка 10 + клей 5 + плитка 9); постирочная — 15 мм (штукатурка 10 + шпаклёвка 5 (принято)); ванная мастер — 24 мм (штукатурка 10 + клей 5 + плитка 9); кухня — 22 мм (фартук: штукатурка 10 + клей 3 + плитка 9)); эти же грани — на развёртках и в раскладке плитки. Высоты — от чистого пола помещения.
2. Высоты и межосевые, отмеченные «*», приняты по практике монтажа; до черновой разводки сверить по паспорту выбранного прибора (смеситель, инсталляция, сифон).
3. Горячая вода (Т3) — слева от холодной (В1), если смотреть на прибор. Допуск установки выводов: ±5 мм в группе, ±20 мм у отдельно стоящих.
4. Расчёт систем водоснабжения и канализации и подбор оборудования выполняет проектная организация; лист задаёт места и высоты выводов.
5. Посудомоечная машина Кх2: кран и слив — отдельными выводами в шкафу мойки (не за машиной), до машины ≤ 1500 мм.
6. Прибор Кх1 мойка кухонная, Кх2 посудомоечная машина взят из расстановки мебели (по шкафу с мойкой).
7. Ст К1-3*, Ст В1-3*, Ст Т3-3* на обмере не показаны: положение принято, не замерено (К-6); положение сверить на объекте до разметки.
8. Стояки в коробах/шахтах не замоноличивать; стояк К1 в коробе — звукоизоляция стояка в коробе без жёсткого контакта с трубой; к арматуре и ревизиям — люк не меньше 300×400.
9. Знак «*» у стояка — положение принято, не замерено (Ст К1-3*, Ст В1-3*, Ст Т3-3*); сверить на объекте до разметки. Реестр: листы 6–7, вопрос К-6.

1000 мм · печать 1:1

Допущения и предложения на листе. Знак «*» принято (замерить). См. лист открытых вопросов (лист 6).

| Изм. | Кол.уч | Лист | № док. | Подп. | Дата | ГД-2026-009-АИ | | | |
|---|---|---|---|---|---|---|---|---|---|
| | | | | | | Квартира 103 м² | | | |
| | | | | | | Общая площадь 100,72* м² · * размеры со скана, не замерены (реестр — л. 6, 7, К-1) | | | |
| Разраб. | | Кырлан А.С. | | | 04.11.26 | Дизайн-проект интерьера | Стадия | Лист | Листов |
| Пров. | | | | | | | РП | 33 | 120 |
| ГИП | | | | | | План выводов сантехники | Кырлан Александр Сергеевич | | |
| Н. контр. | | | | | | М 1:50 | | | |
| Утв. | | | | | | | | | |


выпуск 04.11.2026 № 35b47f1c2a · стр. 38 из 130

# Схема разводки водопровода и канализации


Схемы систем В1, Т3, К1 · трассы принципиальные · уклоны в мм на 1 м · план М 1:200, фрагменты М 1:40

**ПРЕДВАРИТЕЛЬНО · не для производства работ · открыто пунктов: 8 (реестр — л. 6, 7)**

## План квартиры (М 1:200)

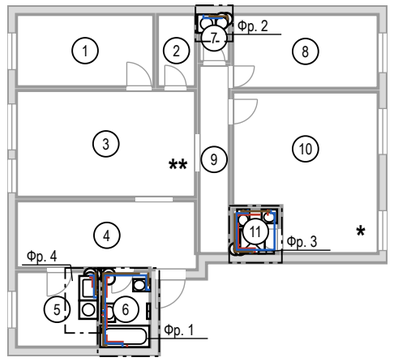


## Узел ввода В1, Т3 (схема, без масштаба)

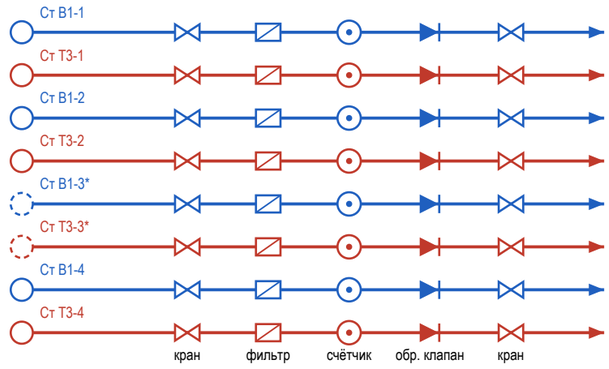



состав узла — по согласованию

⊗ Ст К1-1, Ст К1-2 (кухня), Ст К1-3*, Ст К1-4 (постирочная): ревизия на стояке — люк в коробе


## Условные обозначения

- В1 — водопровод хозяйственно-питьевой (ХВС), PP-R Ø20
- Т3 — горячее водоснабжение, подача (ГВС), PP-R Ø20
- К1 — канализация бытовая
- направление уклона К1 / пола: Ø, мм на 1 м
- ⊗ ревизия (прочистка) К1 — доступ сохранить
- • тройник (ответвление к прибору)
- короб К1 над чистым полом (ГКЛВ под плитку)
- ○ вывод В1 (код — в ведомости привязок)
- ○ вывод Т3 (код — в ведомости привязок)
- ○ вывод К1 (код — в ведомости привязок)
- сантехприбор по расстановке (габарит модели)
- ○ стояк «Ст К1-N / Ст В1-N» (ГОСТ 21.601), Ø мм
- ○ * стояк Т3 не на обмере — принят в шахте рядом со Ст В1, сверить
- * у стояка — положение принято, не замерено, сверить
- линия обрыва (граница фрагмента)
- граница фрагмента на плане (Фр. N)


## Фр. 1. Ванная (М 1:40)

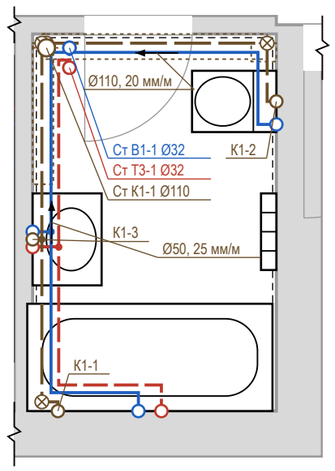



## Фр. 2. Постирочная (М 1:40)

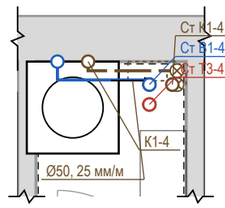


## Фр. 3. Ванная мастер (М 1:40)

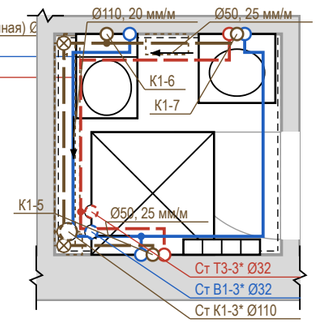


## Фр. 4. Кухня (М 1:40)

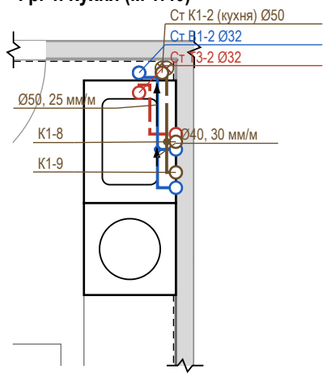


## Профиль выпусков К1 (до врезки в стояк)

| Выпуск | Прибор | Ø | L, м | i, мм/м | Δh, мм | Прокладка, мм |
|---|---|---|---|---|---|---|
| К1-2 | Сн2 унитаз подвесной | Ø110 | 1,91 | 20 | 38 | под проёмом Д-5: короба нет; К-7 |
| К1-6 | См2 унитаз подвесной | Ø110 | 1,60 | 20 | 32 | короб 180×140 |
| К1-1 | Сн1 ванна | Ø50 | 2,56 | 25 | 64 | короб 150×110 |
| К1-7 | См3 умывальник | Ø50 | 2,45 | 25 | 61 | короб 150×110 |
| К1-3 | Сн3 умывальник | Ø50 | 1,40 | 25 | 35 | короб 120×110 |
| К1-4 | Пм1 стиральная машина | Ø50 | 0,76 | 25 | 19 | короб 100×110 |
| К1-5 | См1 душ | Ø50 | 0,76 | 25 | 19 | короб 100×110 |
| К1-8 | Кх1 мойка кухонная | Ø50 | 0,60 | 25 | 15 | над полом за приборами |
| К1-9 | Кх2 посудомоечная машина | Ø40 | 0,80 | 30 | 24 | над полом за приборами |

Короб h×b: h — от чистого пола, b — от чистовой стены. Стяжка 35 мм — лист полов.

## Примечания

1. Трассы принципиальные, построены от стояков вдоль стен помещений; фактическое положение фиксируется исполнительной схемой с привязками (фото с рулеткой) до закрытия.
2. Уклон К1 не менее 1/d и не более 150 мм/м (СП 30.13330.2020, п. 19.1), приняты практические уклоны; поворот — двумя отводами 45°, ревизия после поворота, доступ сохранить. Стояк К1 в коробе — звукоизоляция стояка в коробе, без жёсткого контакта короба с трубой.
3. Решение по К1: стяжка 35 мм не укрывает трубы (нужно Ø + Δh + 45 мм) — выпуски идут над чистым полом вдоль стен: К1-8, К1-9 — за приборами и в раме инсталляции; К1-6, К1-1, К1-7, К1-3, К1-4, К1-5 — в коробе ГКЛВ под плитку (размеры в профиле). Короба — на развёртках; отметку низа врезки в стояк замерить до черновых работ.
4. К1-2 (Сн2 унитаз подвесной): трасса К1 до Ст К1-1 — под проёмом Д-5, короб там не поставить: прибор ближе к стояку, выпуск в полу с подъёмом пола или насосная установка (КНС) — решение К-7; до решения не выполнять.
5. Состав узла ввода В1, Т3 — по согласованию: на схеме типовой узел — кран шаровой, фильтр, счётчик, обратный клапан, кран; состав и места не определены (записи реестра нет). Доступ к арматуре — через люк не меньше 300×400. Водопровод — в штробе стен или в коробах; трубы испытать давлением до закрытия (акт скрытых работ).
6. Расчёт систем, диаметры магистралей и подбор оборудования выполняет проектная организация; врезка и перенос стояков — по согласованию с управляющей организацией. Арматуру и привязки сверить по паспортам приборов.
7. Ст К1-3*, Ст В1-3*, Ст Т3-3* на обмере не показаны: положение принято, не замерено (К-6); положение сверить на объекте до разводки.
8. Знак «*» у стояка — положение принято, не замерено (Ст К1-3*, Ст В1-3*, Ст Т3-3*); сверить на объекте до разметки. Реестр: листы 6–7, вопрос К-6.

Допущения и предложения на листе. Знак «*» принято (замерить). Знак «**» предложено (согласовать). См. лист открытых вопросов (лист 6).

| | | | | | | | | |
|---|---|---|---|---|---|---|---|---|
| | | | | | | **ГД-2026-009-АИ** | | |
| | | | | | | Квартира 103 м² | | |
| | | | | | | Общая площадь 100,72* м² · * размеры со скана, не замерены (реестр — л. 6, 7, К-1) | | |
| Изм. | Кол.уч | Лист | № док. | Подп. | Дата | | | |
| Разраб. | | Кырлан А.С. | | | 04.11.26 | Дизайн-проект интерьера | Стадия: РП | Лист: 34 / Листов: 120 |
| Пров. | | | | | | | | |
| ГИП | | | | | | | | |
| Н. контр. | | | | | | **Схема разводки водопровода и канализации** М 1:200; 1:40 | **Кырлан Александр Сергеевич** | |
| Утв. | | | | | | | | |


выпуск 04.11.2026 № 35b47f1c2a · стр. 39 из 130

# Аксонометрическая схема В1 (холодное водоснабжение)

аксонометрия · диаметры, уклоны, отметки, стояки и приборы · трассы принципиальные

**Схема В1 (М 1:100; по вертикали и горизонтали один масштаб, глубина — ×0,5 под 45°)**

**ПРЕДВАРИТЕЛЬНО · не для производства работ · открыто пунктов: 8 (реестр — л. 6, 7)**

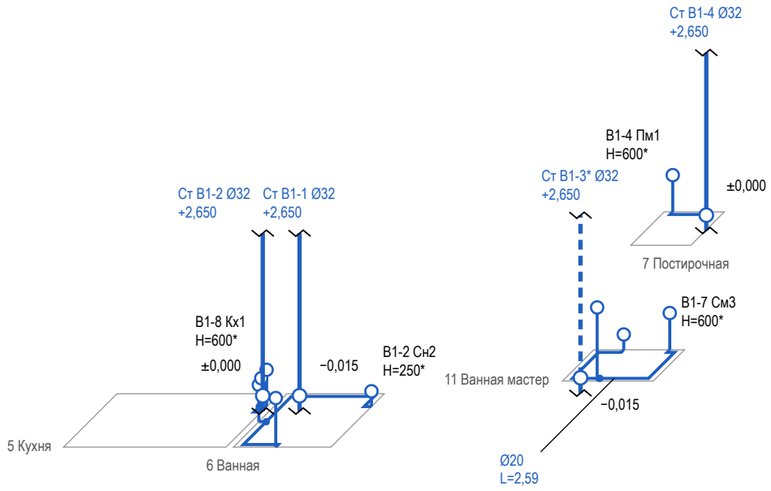


## Условные обозначения

- В1 — водопровод хозяйственно-питьевой (ХВС), PP-R Ø20
- вывод В1 (код — в ведомости привязок)
- стояк «Ст К1-N / Ст В1-N» (ГОСТ 21.601), Ø мм
- стояк в плане (на отметке пола); вертикаль — стояк по высоте, разрыв — перекрытие
- тройник (ответвление к прибору)
- кран шаровой
- * стояк Т3 не на обмере — принят в шахте рядом со Ст В1, сверить

**Допущения и предложения на листе**

Основа листа: размеры сняты со скана обмерного плана KV оформление (см): часть подписей не читается, помещения выровнены по читаемым размерам; контрольный обмер не выполнен (К-1); высота потолка 2650 мм принята по отметкам обмера (Н = 2,50…2,66 м, ригель 2,28 м) — уточнить при обмере (К-2); толщины стен 300 / 120 мм приняты, межквартирная стена и колонны — по скану, не замерены (К-1); разрешённая мощность 15 кВт принята по типовым ТУ; при объединении двух квартир — переоформление ТУ (К-4); подрайон климата не задан — принят не северный (жилые от 2,5 м) (К-8).

Знак «*» — принято, не замерено и не подтверждено (замерить на объекте): К-6: Ст В1-3, Ст К1-3, Ст Т3-3 — положение снято со скана обмера, отдельно не замерялось; ось внутри габарита поддона См1 — обмер угла по К-6.

См. лист открытых вопросов (лист 6, записи К-1, К-2, К-4, К-6, К-8).

## Примечания

1. Схема В1 построена по тем же трассам, что план разводки: положение в плане сохранено, глубина — в масштабе ×0,5. Трассы принципиальные; фактическое положение фиксируется исполнительной схемой до закрытия.
2. Высоты Н — от чистого пола помещения, мм. Отметка прокладки магистрали В1 (в стяжке, в стене или по полу) в данных не задана: участки показаны на уровне пола условно (записи реестра нет).
3. * — высота вывода принята по практике монтажа; сверить по паспорту прибора.
4. Узел ввода В1 (кран, фильтр, счётчик, обратный клапан, кран) — на схеме разводки; состав узла ввода — по согласованию. Кран шаровой — на первом участке от стояка.
5. Ст В1-3* на обмере не показаны: положение принято, не замерено (К-6); положение сверить на объекте до разводки.
6. Трубы испытать давлением до закрытия (акт скрытых работ, опрессовка по СП 73.13330.2016).
7. Диаметры, высоты выводов и места кранов — по паспортам выбранных приборов и расчёту проектной организации.
8. Расчёт систем, диаметры магистралей и подбор оборудования выполняет проектная организация.

1000 мм · печать 1:1

| Изм. | Кол.уч | Лист | № док. | Подп. | Дата |
|---|---|---|---|---|---|
| Разраб. | | Кырлан А.С. | | | 04.11.26 |
| Пров. | | | | | |
| ГИП | | | | | |
| | | | | | |
| Н. контр. | | | | | |
| Утв. | | | | | |

**ГД-2026-009-АИ**

Квартира 103 м²

Общая площадь 100,72* м² · * размеры со скана, не замерены (реестр — л. 6, 7, К-1)


| Дизайн-проект интерьера | Стадия | Лист | Листов |
|---|---|---|---|
| | РП | 35 | 120 |
| **Аксонометрическая схема В1 (холодное водоснабжение)** М 1:100 | **Кырлан Александр Сергеевич** | | |

выпуск 04.11.2026 № 35b47f1c2a · стр. 40 из 130

# Аксонометрическая схема Т3 (горячее водоснабжение)

аксонометрия · диаметры, уклоны, отметки, стояки и приборы · трассы принципиальные

**Схема Т3 (М 1:100; по вертикали и горизонтали один масштаб, глубина — ×0,5 под 45°)**

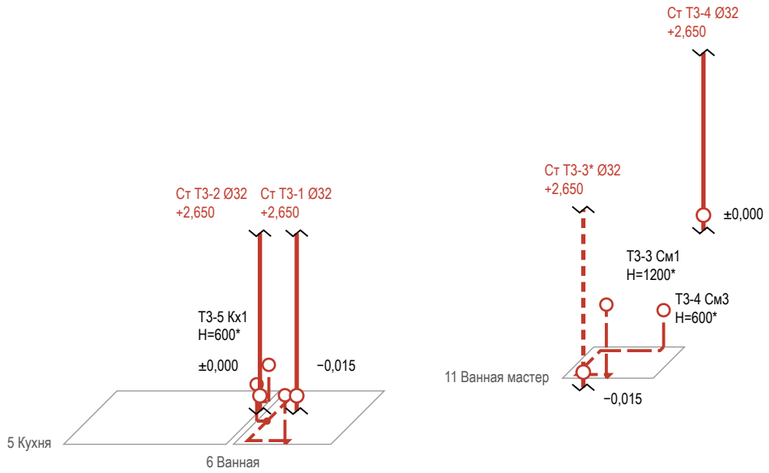


**ПРЕДВАРИТЕЛЬНО · не для производства работ · открыто пунктов: 8 (реестр — л. 6, 7)**

## Условные обозначения

- Т3 — горячее водоснабжение, подача (ГВС), PP-R Ø20
- вывод Т3 (код — в ведомости привязок)
- стояк «Ст К1-N / Ст В1-N» (ГОСТ 21.601), Ø мм
- стояк в плане (на отметке пола); вертикаль — стояк по высоте, разрыв — перекрытие
- тройник (ответвление к прибору)
- кран шаровой
- * стояк Т3 не на обмере — принят в шахте рядом со Ст В1, сверить

**Допущения и предложения на листе**

Основа листа: размеры сняты со скана обмерного плана KV оформление (см): часть подписей не читается, помещения выровнены по читаемым размерам; контрольный обмер не выполнен (К-1); высота потолка 2650 мм принята по отметкам обмера (Н = 2,50…2,66 м, ригель 2,28 м) — уточнить при обмере (К-2); толщины стен 300 / 120 мм приняты, межквартирная стена и колонны — по скану, не замерены (К-1); разрешённая мощность 15 кВт принята по типовым ТУ; при объединении двух квартир — переоформление ТУ (К-4); подрайон климата не задан — принят не северный (жилые от 2,5 м) (К-8).

Знак «*» — принято, не замерено и не подтверждено (замерить на объекте): К-6: Ст Т3-3, Ст К1-3, Ст В1-3 — положение снято со скана обмера, отдельно не замерялось; ось внутри габарита поддона См1 — обмер угла по К-6.

См. лист открытых вопросов (лист 6, записи К-1, К-2, К-4, К-6, К-8).

## Примечания

1. Схема Т3 построена по тем же трассам, что план разводки: положение в плане сохранено, глубина — в масштабе ×0,5. Трассы принципиальные; фактическое положение фиксируется исполнительной схемой до закрытия.
2. Высоты Н — от чистого пола помещения, мм. Отметка прокладки магистрали Т3 (в стяжке, в стене или по полу) в данных не задана: участки показаны на уровне пола условно (записи реестра нет).
3. * — высота вывода принята по практике монтажа; сверить по паспорту прибора.
4. Узел ввода Т3 (кран, фильтр, счётчик, обратный клапан, кран) — на схеме разводки; состав узла ввода — по согласованию. Кран шаровой — на первом участке от стояка.
5. Циркуляция ГВС в данных не задана — циркуляционного трубопровода на схеме нет (записи реестра нет).
6. Ст Т3-3* на обмере не показаны: положение принято, не замерено (К-6); положение сверить на объекте до разводки.
7. Трубы испытать давлением до закрытия (акт скрытых работ, опрессовка по СП 73.13330.2016).
8. Диаметры, высоты выводов и места кранов — по паспортам выбранных приборов и расчёту проектной организации.
9. Расчёт систем, диаметры магистралей и подбор оборудования выполняет проектная организация.

1000 мм · печать 1:1

| Изм. | Кол.уч | Лист | № док. | Подп. | Дата |
|---|---|---|---|---|---|
| Разраб. | | Кырлан А.С. | | | 04.11.26 |
| Пров. | | | | | |
| ГИП | | | | | |
| | | | | | |
| Н. контр. | | | | | |
| Утв. | | | | | |

**ГД-2026-009-АИ**

Квартира 103 м²

Общая площадь 100,72* м² · * размеры со скана, не замерены (реестр — л. 6, 7, К-1)


| Дизайн-проект интерьера | Стадия | Лист | Листов |
|---|---|---|---|
| | РП | 36 | 120 |
| **Аксонометрическая схема Т3 (горячее водоснабжение)** М 1:100 | **Кырлан Александр Сергеевич** | | |

выпуск 04.11.2026 № 35b47f1c2a · стр. 41 из 130

# Аксонометрическая схема К1 (канализация)

аксонометрия · диаметры, уклоны, отметки, стояки и приборы · трассы принципиальные

**Схема К1 (М 1:100; по вертикали и горизонтали один масштаб, глубина — ×0,5 под 45°)**

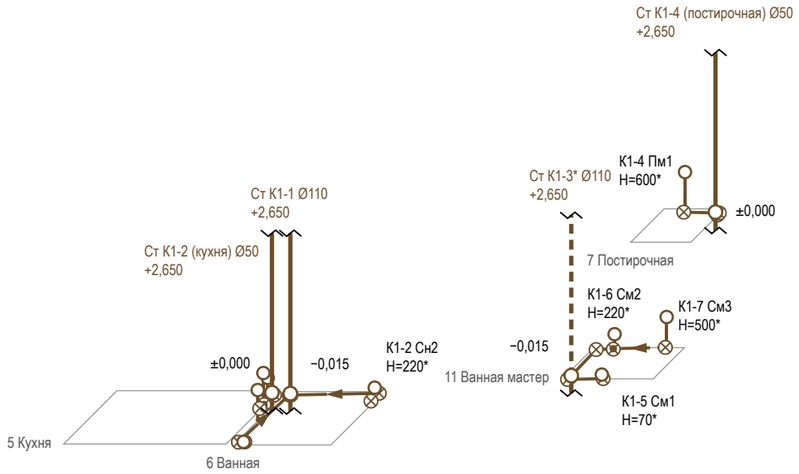


## Условные обозначения

- К1 — канализация бытовая
- вывод К1 (код — в ведомости привязок)
- стояк «Ст К1-N / Ст В1-N» (ГОСТ 21.601), Ø мм
- стояк в плане (на отметке пола); вертикаль — стояк по высоте, разрыв — перекрытие
- направление уклона К1 / пола: Ø, мм на 1 м
- ревизия (прочистка) К1 — доступ сохранить
- тройник (ответвление к прибору)
- * стояк Т3 не на обмере — принят в шахте рядом со Ст В1, сверить

**Допущения и предложения на листе**

Основа листа: размеры сняты со скана обмерного плана KV оформление (см): часть подписей не читается, помещения выровнены по читаемым размерам; контрольный обмер не выполнен (К-1); высота потолка 2650 мм принята по отметкам обмера (Н = 2,50…2,66 м, ригель 2,28 м) — уточнить при обмере (К-2); толщины стен 300 / 120 мм приняты, межквартирная стена и колонны — по скану, не замерены (К-1); разрешённая мощность 15 кВт принята по типовым ТУ; при объединении двух квартир — переоформление ТУ (К-4); подрайон климата не задан — принят не северный (жилые от 2,5 м) (К-8).

Знак «*» — принято, не замерено и не подтверждено (замерить на объекте): К-6: Ст К1-3, Ст В1-3, Ст Т3-3 — положение снято со скана обмера, отдельно не замерялось; ось внутри габарита поддона См1 — обмер угла по К-6.

См. лист открытых вопросов (лист 6, записи К-1, К-2, К-4, К-6, К-8).

## Примечания

1. Схема К1 построена по тем же трассам, что план разводки: положение в плане сохранено, глубина — в масштабе ×0,5. Трассы принципиальные; фактическое положение фиксируется исполнительной схемой до закрытия.
2. Отметки — от плиты перекрытия: низ трубы у врезки в стояк — отметка из данных выпуска, к прибору труба поднимается на уклон i, мм/м (уклон не менее 1/d и не более 150 мм/м, СП 30.13330.2020, п. 19.1); чистый пол — выше плиты на стяжку (высота пирога пола). Высота выпуска прибора Н — от чистого пола.
3. * — высота вывода принята по практике монтажа; сверить по паспорту прибора.
4. Ревизия — на повороте и в начале участка; стояк К1 в коробе с люком — звукоизоляция стояка в коробе; поворот — двумя отводами 45°.
5. Ст К1-3* на обмере не показаны: положение принято, не замерено (К-6); положение сверить на объекте до разводки.
6. Трубы испытать давлением до закрытия (акт скрытых работ, опрессовка по СП 73.13330.2016).
7. Диаметры, высоты выводов и места кранов — по паспортам выбранных приборов и расчёту проектной организации.
8. Расчёт систем, диаметры магистралей и подбор оборудования выполняет проектная организация.

1000 мм · печать 1:1

ПРЕДВАРИТЕЛЬНО · не для производства работ · открыто пунктов: 8 (реестр — л. 6, 7)

| Изм. | Кол.уч | Лист | № док. | Подп. | Дата |
|---|---|---|---|---|---|
| Разраб. | | Кырлан А.С. | | | 04.11.26 |
| Пров. | | | | | |
| ГИП | | | | | |
| | | | | | |
| Н. контр. | | | | | |
| Утв. | | | | | |

**ГД-2026-009-АИ**

Квартира 103 м²

Общая площадь 100,72* м² · * размеры со скана, не замерены (реестр — л. 6, 7, К-1)

| Дизайн-проект интерьера | Стадия | Лист | Листов |
|---|---|---|---|
| | РП | 37 | 120 |

**Аксонометрическая схема К1 (канализация)**

М 1:100

**Кырлан Александр Сергеевич**


выпуск 04.11.2026 № 35b47f1c2a · стр. 42 из 130

# Развёртки мокрых зон: выводы ВК. Кухня

пом. 5 · выводы В1, Т3, К1 на стенах · высоты от чистого пола, привязки от чистовых углов, мм

ПРЕДВАРИТЕЛЬНО · не для производства работ · открыто пунктов: 8 (реестр — л. 6, 7)

### Стена Б (М 1:20)

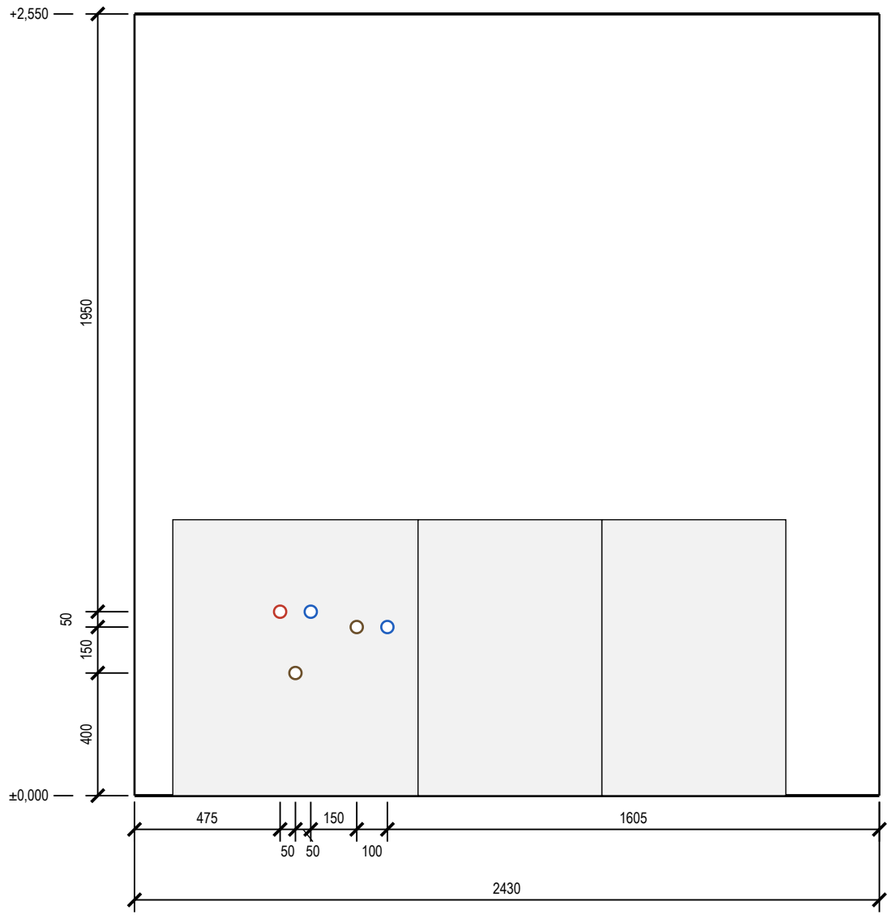


**Допущения и предложения на листе**

Основа листа: размеры сняты со скана обмерного плана KV оформление (см): часть подписей не читается, помещения выровнены по читаемым размерам; контрольный обмер не выполнен (К-1); высота потолка 2650 мм принята по отметкам обмера (Н = 2,50…2,66 м, ригель 2,28 м) — уточнить при обмере (К-2); толщины стен 300 / 120 мм приняты, межквартирная стена и колонны — по скану, не замерены (К-1); разрешённая мощность 15 кВт принята по типовым ТУ; при объединении двух квартир — переоформление ТУ (К-4); подрайон климата не задан — принят не северный (жилые от 2,5 м) (К-8).

См. лист открытых вопросов (лист 6, записи К-1, К-2, К-4, К-8).

### Ведомость привязок выводов (от чистого пола и угла)

| Код | Прибор | Ø | Н, мм | Привязка, мм |
|---|---|---|---|---|
| В1-8 | Кх1 мойка кухонная | ½" | 600* | ст. Б: 575 от лев. угла |
| Т3-5 | Кх1 мойка кухонная | ½" | 600* | ст. Б: 475 от лев. угла |
| К1-8 | Кх1 мойка кухонная | Ø50 | 400* | ст. Б: 525 от лев. угла |

### Ведомость привязок (продолжение)

| Код | Прибор | Ø | Н, мм | Привязка, мм |
|---|---|---|---|---|
| В1-9 | Кх2 посудомоечная машина | ½" | 550* | ст. Б: 825 от лев. угла |
| К1-9 | Кх2 посудомоечная машина | Ø40 | 550* | ст. Б: 725 от лев. угла |

### Условные обозначения

- вывод В1 (код — в ведомости привязок)
- вывод Т3 (код — в ведомости привязок)
- вывод К1 (код — в ведомости привязок)
- сантехприбор по расстановке (габарит модели)
- дверной проём; окно — сплошной контур

### Примечания

1. Габариты и высоты приборов, межосевые смесителей и места кранов — по паспортам выбранных приборов, сверяются до разметки стен.
2. Высоты Н — от чистого пола помещения, мм; отметка чистого пола и потолка — у левого края вида (от ±0,000 объекта). Привязки — от левого чистового угла вида (облицовка стен вычтена), как на развёртках стен.
3. * — высота принята по практике монтажа: в данных прибора её нет; до разметки стен сверить по паспорту выбранного прибора (смеситель, инсталляция, сифон).
4. Стояки в помещении: Ст К1-2 (кухня) Ø50, Ст В1-2 Ø32, Ст Т3-2 Ø32 — положение на плане выводов; выводы подключаются к ним по схеме разводки.
5. Ревизионные люки к арматуре и ревизиям в данных не заданы: место и размер не определены (записи реестра нет).
6. Мойка, ПММ и фильтр — выводы в шкафу мойки; диаметры и положение сифона и кранов сверить по паспортам приборов и чертежам модуля.
7. Часть подписей выводов не уместилась у знака: коды и высоты — в ведомости привязок.
8. Расчёт систем водоснабжения и канализации и подбор оборудования выполняет проектная организация; лист задаёт места и высоты выводов.

1000 мм · печать 1:1

| Изм. | Кол.уч | Лист | № док. | Подп. | Дата |
|---|---|---|---|---|---|
| Разраб. | | Кырлан А.С. | | | 04.11.26 |
| Пров. | | | | | |
| ГИП | | | | | |
| | | | | | |
| Н. контр. | | | | | |
| Утв. | | | | | |

**ГД-2026-009-АИ**

Квартира 103 м²

Общая площадь 100,72* м² · * размеры со скана, не замерены (реестр — л. 6, 7, К-1)

Дизайн-проект интерьера

| Стадия | Лист | Листов |
|---|---|---|
| РП | 38 | 120 |

**Развёртки мокрых зон: выводы ВК. Кухня**

М 1:20

**Кырлан Александр Сергеевич**


выпуск 04.11.2026 № 35b47f1c2a · стр. 43 из 130

# Развёртки мокрых зон: выводы ВК. Ванная


пом. 6 · выводы В1, Т3, К1 на стенах · высоты от чистого пола, привязки от чистовых углов, мм

ПРЕДВАРИТЕЛЬНО · не для производства работ · открыто пунктов: 8 (реестр — л. 6, 7)


### Стена Б (М 1:25)

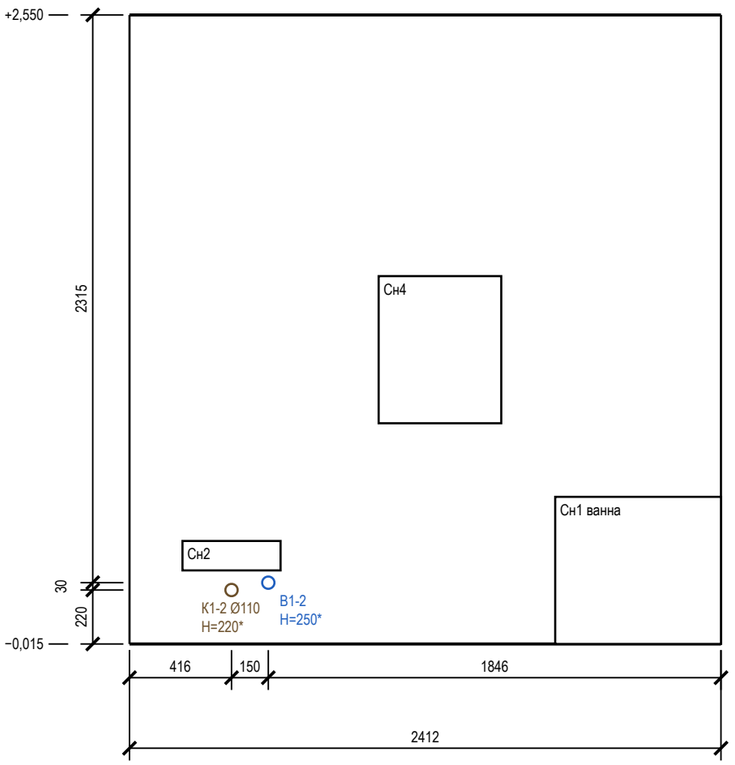


### Стена В (М 1:25)

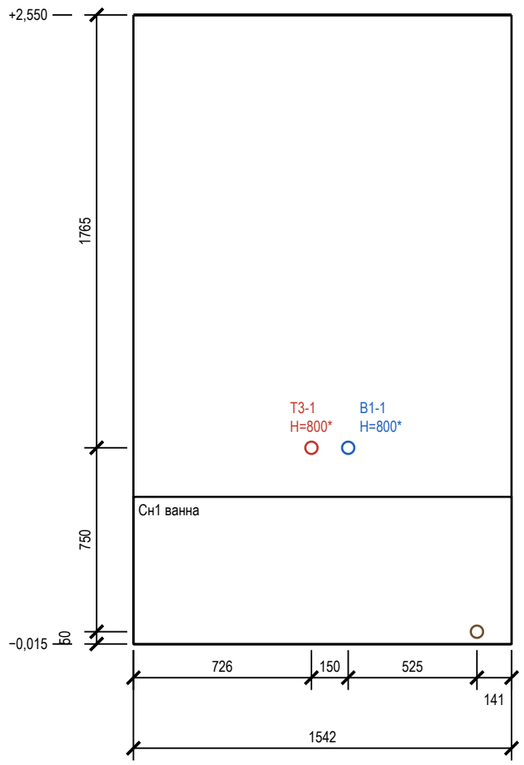


### Стена Г (М 1:25)

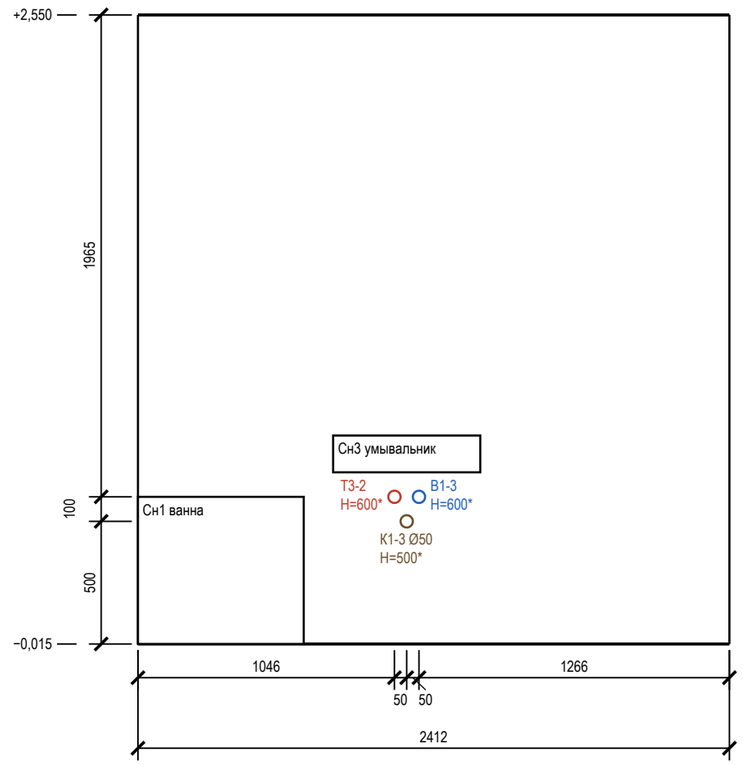


## Ведомость привязок выводов (от чистого пола и угла)

| Код | Прибор | Ø | H, мм | Привязка, мм |
|---|---|---|---|---|
| В1-2 | Сн2 унитаз подвесной | ½" | 250* | ст. Б: 566 от лев. угла |
| К1-2 | Сн2 унитаз подвесной | Ø110 | 220* | ст. Б: 416 от лев. угла |
| В1-1 | Сн1 ванна | ½" | 800* | ст. В: 876 от лев. угла |
| Т3-1 | Сн1 ванна | ½" | 800* | ст. В: 726 от лев. угла |
| К1-1 | Сн1 ванна | Ø50 | 50* | ст. В: 1401 от лев. угла |
| В1-3 | Сн3 умывальник | ½" | 600* | ст. Г: 1146 от лев. угла |
| Т3-2 | Сн3 умывальник | ½" | 600* | ст. Г: 1046 от лев. угла |
| К1-3 | Сн3 умывальник | Ø50 | 500* | ст. Г: 1096 от лев. угла |

## Условные обозначения

- вывод В1 (код — в ведомости привязок)
- вывод Т3 (код — в ведомости привязок)
- вывод К1 (код — в ведомости привязок)
- сантехприбор по расстановке (габарит модели)
- дверной проём; окно — сплошной контур

**Допущения и предложения на листе**

Основа листа: размеры сняты со скана обмерного плана KV оформление (см): часть подписей не читается, помещения выровнены по читаемым размерам; контрольный обмер не выполнен (К-1); высота потолка 2650 мм принята по отметкам обмера (Н = 2,50…2,66 м, ригель 2,28 м) — уточнить при обмере (К-2); толщины стен 300 / 120 мм приняты, межквартирная стена и колонны — по скану, не замерены (К-1); разрешённая мощность 15 кВт принята по типовым ТУ; при объединении двух квартир — переоформление ТУ (К-4); подрайон климата не задан — принят не северный (жилые от 2,5 м) (К-8). См. лист открытых вопросов (лист 6, записи К-1, К-2, К-4, К-8).

## Примечания

1. Габариты и высоты приборов, межосевые смесителей и места кранов — по паспортам выбранных приборов, сверяются до разметки стен.
2. Высоты Н — от чистого пола помещения, мм; отметка чистого пола и потолка — у левого края вида (от ±0,000 объекта). Привязки — от левого чистового угла вида (облицовка стен вычтена), как на развёртках стен.
3. * — высота принята по практике монтажа: в данных прибора её нет; до разметки стен сверить по паспорту выбранного прибора (смеситель, инсталляция, сифон).
4. Стояки в помещении: Ст К1-1 Ø110, Ст В1-1 Ø32, Ст Т3-1 Ø32 — положение на плане выводов; выводы подключаются к ним по схеме разводки.
5. Ревизионные люки к арматуре и ревизиям в данных не заданы: место и размер не определены (записи реестра нет).
6. Часть подписей выводов не уместилась у знака: коды и высоты — в ведомости привязок.
7. Расчёт систем водоснабжения и канализации и подбор оборудования выполняет проектная организация; лист задаёт места и высоты выводов.

1000 мм · печать 1:1

| Изм. | Кол.уч | Лист | № док. | Подп. | Дата |
|---|---|---|---|---|---|
| Разраб. | | Кырлан А.С. | | | 04.11.26 |
| Пров. | | | | | |
| ГИП | | | | | |
| | | | | | |
| Н. контр. | | | | | |
| Утв. | | | | | |

**ГД-2026-009-АИ**

Квартира 103 м²

Общая площадь 100,72* м² · * размеры со скана, не замерены (реестр — л. 6, 7, К-1)

Дизайн-проект интерьера

| Стадия | Лист | Листов |
|---|---|---|
| РП | 39 | 120 |

**Развёртки мокрых зон: выводы ВК. Ванная**

М 1:25

**Кырлан Александр Сергеевич**


выпуск 04.11.2026 № 35b47f1c2a · стр. 44 из 130

# Развёртки мокрых зон: выводы ВК. Постирочная


пом. 7 · выводы В1, Т3, К1 на стенах · высоты от чистого пола, привязки от чистовых углов, мм

**ПРЕДВАРИТЕЛЬНО · не для производства работ · открыто пунктов: 8 (реестр — л. 6, 7)**

### Стена А (М 1:20)

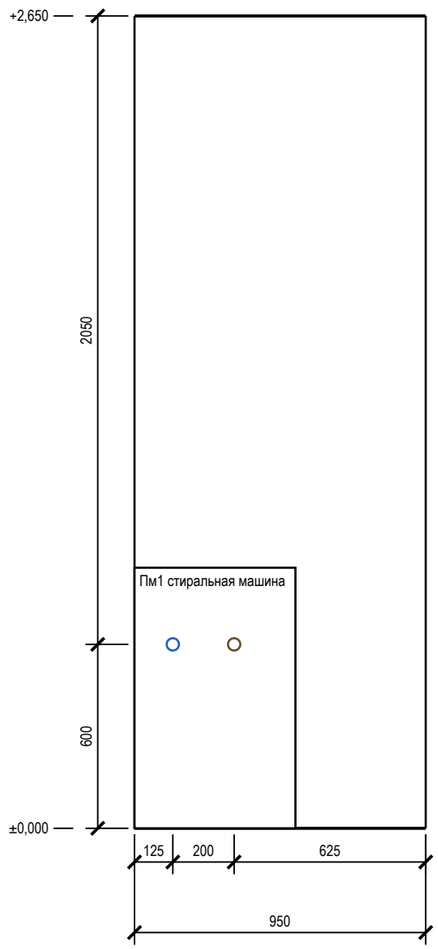


### Стена Г (М 1:20)

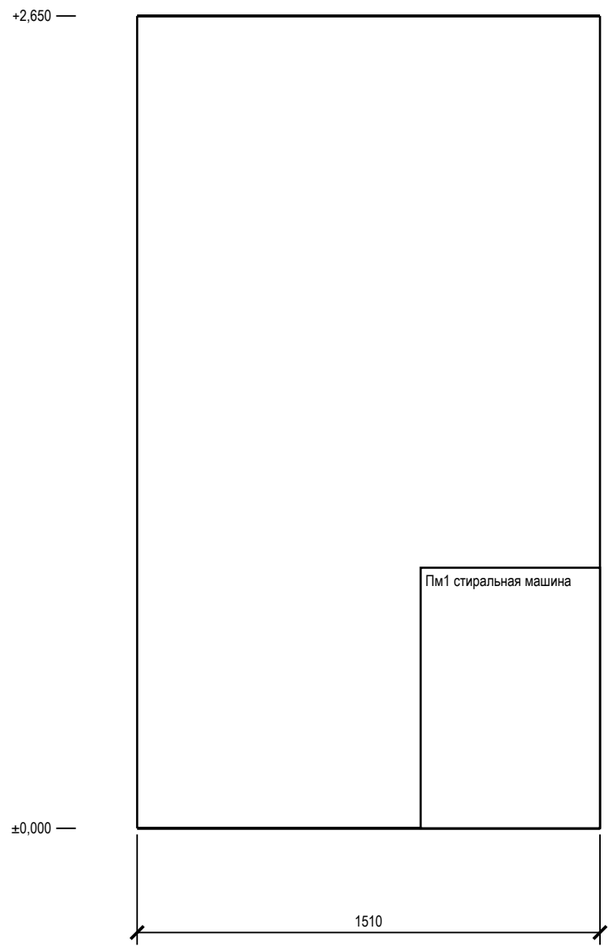


**Допущения и предложения на листе**

Основа листа: размеры сняты со скана обмерного плана KV оформление (см): часть подписей не читается, помещения выровнены по читаемым размерам; контрольный обмер не выполнен (К-1); высота потолка 2650 мм принята по отметкам обмера (Н = 2,50…2,66 м, ригель 2,28 м) — уточнить при обмере (К-2); толщины стен 300 / 120 мм приняты, межквартирная стена и колонны — по скану, не замерены (К-1); разрешённая мощность 15 кВт принята по типовым ТУ; при объединении двух квартир — переоформление ТУ (К-4); подрайон климата не задан — принят не северный (жилые от 2,5 м) (К-8).

См. лист открытых вопросов (лист 6, записи К-1, К-2, К-4, К-8).

## Ведомость привязок выводов (от чистого пола и угла)

| Код | Прибор | Ø | Н, мм | Привязка, мм |
|---|---|---|---|---|
| В1-4 | Пм1 стиральная машина | ½" | 600* | ст. А: 125 от лев. угла |
| К1-4 | Пм1 стиральная машина | Ø50 | 600* | ст. А: 325 от лев. угла |

## Условные обозначения

- вывод В1 (код — в ведомости привязок)
- вывод Т3 (код — в ведомости привязок)
- вывод К1 (код — в ведомости привязок)
- сантехприбор по расстановке (габарит модели)
- дверной проём; окно — сплошной контур

## Примечания

1. Габариты и высоты приборов, межосевые смесителей и места кранов — по паспортам выбранных приборов, сверяются до разметки стен.
2. Высоты Н — от чистого пола помещения, мм; отметка чистого пола и потолка — у левого края вида (от ±0,000 объекта). Привязки — от левого чистового угла вида (облицовка стен вычтена), как на развёртках стен.
3. * — высота принята по практике монтажа: в данных прибора её нет; до разметки стен сверить по паспорту выбранного прибора (смеситель, инсталляция, сифон).
4. Стояки в помещении: Ст К1-4 (постирочная) Ø50, Ст В1-4 Ø32, Ст Т3-4 Ø32 — положение на плане выводов; выводы подключаются к ним по схеме разводки.
5. Ревизионные люки к арматуре и ревизиям в данных не заданы: место и размер не определены (записи реестра нет).
6. Часть подписей выводов не уместилась у знака: коды и высоты — в ведомости привязок.
7. Расчёт систем водоснабжения и канализации и подбор оборудования выполняет проектная организация; лист задаёт места и высоты выводов.

1000 мм · печать 1:1

| Изм. | Кол.уч | Лист | № док. | Подп. | Дата |
|---|---|---|---|---|---|
| Разраб. | | Кырлан А.С. | | | 04.11.26 |
| Пров. | | | | | |
| ГИП | | | | | |
| | | | | | |
| Н. контр. | | | | | |
| Утв. | | | | | |

**ГД-2026-009-АИ**

Квартира 103 м²

Общая площадь 100,72* м² · * размеры со скана, не замерены (реестр — л. 6, 7, К-1)

Дизайн-проект интерьера

| Стадия | Лист | Листов |
|---|---|---|
| РП | 40 | 120 |

**Развёртки мокрых зон: выводы ВК. Постирочная**

М 1:20

**Кырлан Александр Сергеевич**


выпуск 04.11.2026 № 35b47f1c2a · стр. 45 из 130

# Развёртки мокрых зон: выводы ВК. Ванная мастер


пом. 11 · выводы В1, Т3, К1 на стенах · высоты от чистого пола, привязки от чистовых углов, мм

**ПРЕДВАРИТЕЛЬНО · не для производства работ · открыто пунктов: 8 (реестр — л. 6, 7)**


### Стена А (М 1:20)

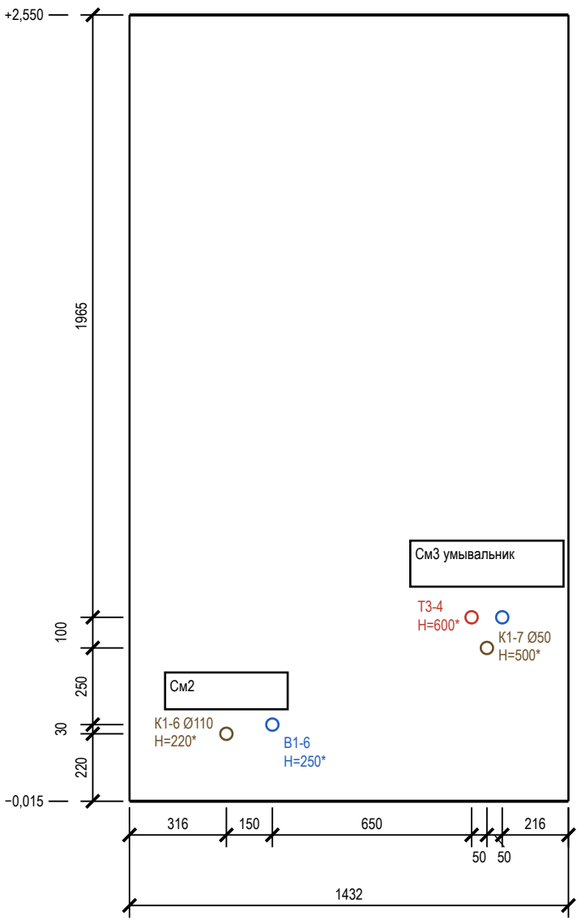


### Стена Б (М 1:20)

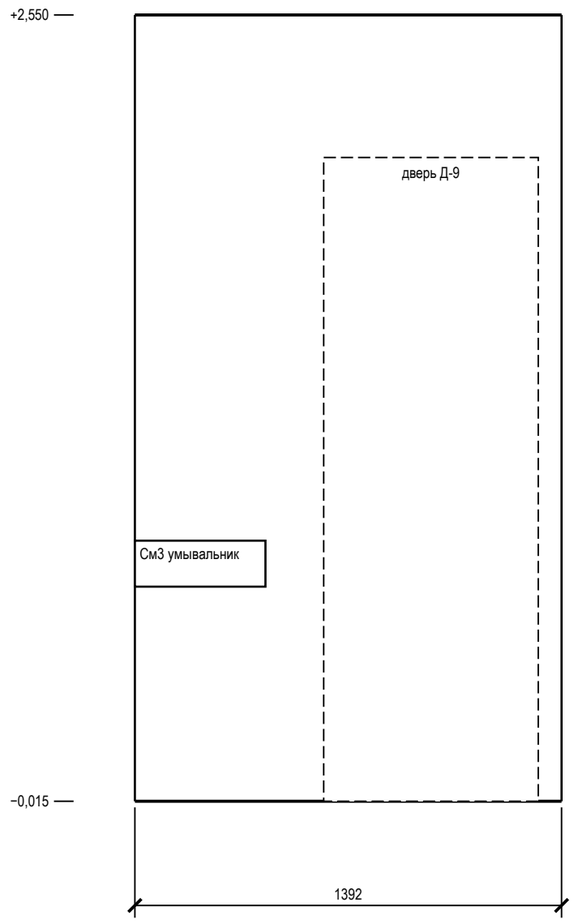


### Стена В (М 1:20)

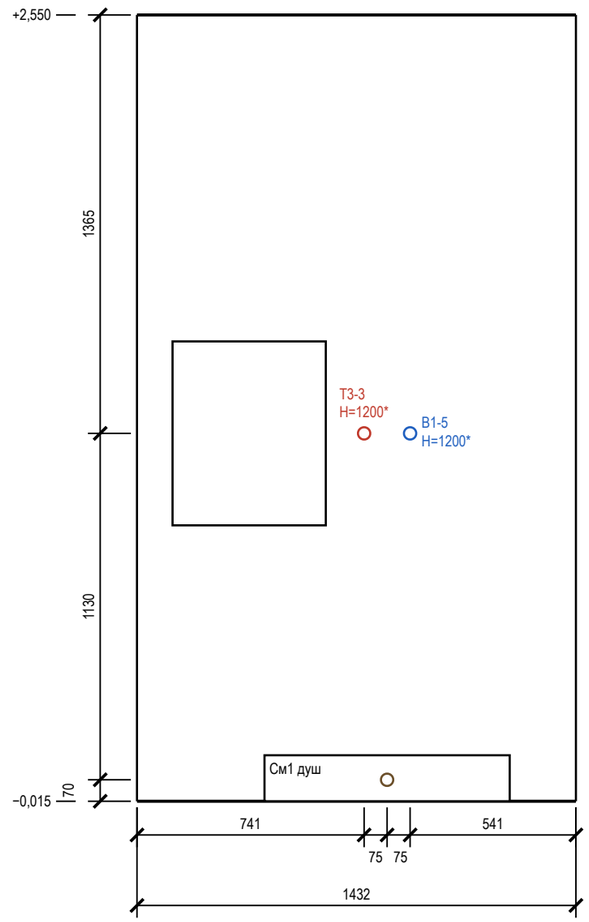


**Допущения и предложения на листе**

Основа листа: размеры сняты со скана обмерного плана KV оформление (см): часть подписей не читается, помещения выровнены по читаемым размерам; контрольный обмер не выполнен (К-1); высота потолка 2650 мм принята по отметкам обмера (Н = 2,50…2,66 м, ригель 2,28 м) — уточнить при обмере (К-2); толщины стен 300 / 120 мм приняты, межквартирная стена и колонны — по скану, не замерены (К-1); разрешённая мощность 15 кВт принята по типовым ТУ; при объединении двух квартир — переоформление ТУ (К-4); подрайон климата не задан — принят не северный (жилые от 2,5 м) (К-8).

Знак «*» — принято, не замерено и не подтверждено (замерить на объекте): К-6: Ст К1-3, Ст В1-3, Ст Т3-3 — положение снято со скана обмера, отдельно не замерялось; ось внутри габарита поддона См1 — обмер угла по К-6.

См. лист открытых вопросов (лист 6, записи К-1, К-2, К-4, К-6, К-8).

### Ведомость привязок выводов (от чистого пола и угла)

| Код | Прибор | Ø | Н, мм | Привязка, мм |
|---|---|---|---|---|
| В1-6 | См2 унитаз подвесной | ½" | 250* | ст. А: 466 от лев. угла |
| К1-6 | См2 унитаз подвесной | Ø110 | 220* | ст. А: 316 от лев. угла |
| В1-7 | См3 умывальник | ½" | 600* | ст. А: 1216 от лев. угла |
| Т3-4 | См3 умывальник | ½" | 600* | ст. А: 1116 от лев. угла |

### Ведомость привязок (продолжение)

| Код | Прибор | Ø | Н, мм | Привязка, мм |
|---|---|---|---|---|
| К1-7 | См3 умывальник | Ø50 | 500* | ст. А: 1166 от лев. угла |
| В1-5 | См1 душ | ½" | 1200* | ст. В: 891 от лев. угла |
| Т3-3 | См1 душ | ½" | 1200* | ст. В: 741 от лев. угла |
| К1-5 | См1 душ | Ø50 | 70* | ст. В: 816 от лев. угла |

### Условные обозначения

- вывод В1 (код — в ведомости привязок)
- вывод Т3 (код — в ведомости привязок)
- вывод К1 (код — в ведомости привязок)
- сантехприбор по расстановке (габарит модели)
- дверной проём; окно — сплошной контур

### Примечания

1. Габариты и высоты приборов, межосевые смесителей и места кранов — по паспортам выбранных приборов, сверяются до разметки стен.
2. Высоты Н — от чистого пола помещения, мм; отметка чистого пола и потолка — у левого края вида (от ±0,000 объекта). Привязки — от левого чистового угла вида (облицовка стен вычтена), как на развёртках стен.
3. * — высота принята по практике монтажа: в данных прибора её нет; до разметки стен сверить по паспорту выбранного прибора (смеситель, инсталляция, сифон).
4. Стояки в помещении: Ст К1-3* Ø110, Ст В1-3* Ø32, Ст Т3-3* Ø32 — положение на плане выводов; выводы подключаются к ним по схеме разводки.
5. Ревизионные люки к арматуре и ревизиям в данных не заданы: место и размер не определены (записи реестра нет).
6. Часть подписей выводов не уместилась у знака: коды и высоты — в ведомости привязок.
7. Расчёт систем водоснабжения и канализации и подбор оборудования выполняет проектная организация; лист задаёт места и высоты выводов.

1000 мм · печать 1:1

| Изм. | Кол.уч | Лист | № док. | Подп. | Дата |
|---|---|---|---|---|---|
| Разраб. | | Кырлан А.С. | | | 04.11.26 |
| Пров. | | | | | |
| ГИП | | | | | |
| | | | | | |
| Н. контр. | | | | | |
| Утв. | | | | | |

**ГД-2026-009-АИ**

Квартира 103 м²

Общая площадь 100,72* м² · * размеры со скана, не замерены (реестр — л. 6, 7, К-1)

Дизайн-проект интерьера

| Стадия | Лист | Листов |
|---|---|---|
| РП | 41 | 120 |

**Развёртки мокрых зон: выводы ВК. Ванная мастер**

М 1:20

**Кырлан Александр Сергеевич**

выпуск 04.11.2026 № 35b47f1c2a · стр. 46 из 130

# Спецификация сантехнического оборудования

Форма 1 ГОСТ 21.110-2013 · ГД-2026-009-АИ-ВК.СО · приборы, арматура, трубопроводы

**ПРЕДВАРИТЕЛЬНО · не для производства работ · открыто пунктов: 8 (реестр — л. 6, 7)**

| Поз. | Наименование и техническая характеристика | Тип, марка, обозначение документа | Код продукции | Поставщик | Ед. изм. | Кол. | Масса 1 ед., кг | Примечание |
|---|---|---|---|---|---|---|---|---|
| | Санитарные приборы | | | | | | | |
| 1 | Ванна встраиваемая акриловая 1600×700 мм, с каркасом, экраном и отверстием слив-перелив | аналог | | выбор заказчика | шт | 1 | | Сн1 |
| 2 | Унитаз подвесной безободковый, с сиденьем микролифт, крепёж и звукоизолирующая прокладка | Jacob Delafon Struktura EDF102-00 | | выбор заказчика | шт | 2 | | Сн2, См2 |
| 3 | Инсталляция для подвесного унитаза: рама высотой 1120 мм, бачок, клавиша смыва (ось клавиши 1050 мм от чистого пола) | аналог | | выбор заказчика | шт | 2 | | Сн2, См2; короб ГКЛВ |
| 4 | Умывальник подвесной 600×450 мм, с отверстием под смеситель и переливом | аналог | | выбор заказчика | шт | 1 | | Сн3 |
| 5 | Умывальник подвесной 500×450 мм, с отверстием под смеситель и переливом | аналог | | выбор заказчика | шт | 1 | | См3 |
| 6 | Поддон душевой низкий 800×800 мм, с сифоном и выпуском Ø50, на ножках/подиуме | аналог | | выбор заказчика | шт | 1 | | См1 |
| 7 | Мойка кухонная врезная / подстольная, с переливом, ориентир 700×480 мм — в модуле Кх1 шириной 800 мм, вырез по шаблону модели | аналог | | с кухонной мебелью | шт | 1 | | Кх1 |
| 8 | Полотенцесушитель электрический, IP44, с терморегулятором | аналог | | выбор заказчика | шт | 2 | | Сн4, См4 |
| | Смесители, сифоны и арматура приборов | | | | | | | |
| 9 | Смеситель для ванны настенный однорычажный, межосевое 150 мм, с душевым набором (лейка, шланг, держатель) | аналог | | выбор заказчика | шт | 1 | | Сн1 |
| 10 | Смеситель для умывальника однорычажный, с донным клапаном | аналог | | выбор заказчика | шт | 2 | | Сн3, См3 |
| 11 | Душевая система скрытого монтажа с термостатом: встраиваемая часть, верхний душ, ручная лейка | аналог | | выбор заказчика | шт | 1 | | См1; встраиваемая часть — до плитки |
| 12 | Смеситель кухонный однорычажный, высокий излив | аналог | | выбор заказчика | шт | 1 | | Кх1 |
| 13 | Обвязка ванны слив-перелив Ø40/50 с сифоном | аналог | | выбор заказчика | шт | 1 | | Сн1 |
| 14 | Сифон для умывальника бутылочный Ø32/40–50, с гофрой к выпуску | аналог | | выбор заказчика | шт | 2 | | Сн3, См3 |
| 15 | Сифон для мойки Ø40/50 | аналог | | выбор заказчика | шт | 1 | | Кх1 |
| 16 | Сифон для посудомоечной машины с обратным клапаном, на выводе слива Ø40 | аналог | | выбор заказчика | шт | 1 | | Кх2 |
| 17 | Сифон для стиральной машины встраиваемый в стену Ø50, с обратным клапаном | аналог | | выбор заказчика | шт | 1 | | Пм1 |
| 18 | Кран угловой ½"×½" с гибкой подводкой 40 см (умывальники, мойка) | аналог | | выбор заказчика | шт | 6 | | по 2 на прибор |
| 19 | Кран шаровой угловой ½"×¾" для подключения стиральной и посудомоечной машины | аналог | | выбор заказчика | шт | 2 | | Пм1, Кх2 |
| | Трубопроводы | | | | | | | |
| 20 | Труба полипропиленовая PP-R PN20 Ø20×3,4 (В1) | ГОСТ 32415-2013 | | выбор заказчика | м | 19 | 0,17 | 11,4 + 5,5 + 10 % |
| 21 | Труба PP-R, армированная стекловолокном, PN20 Ø20×2,8 (Т3) | ГОСТ 32415-2013 | | выбор заказчика | м | 12 | 0,15 | 6,9 + 3,8 + 10 % |
| 22 | Труба канализационная ПП Ø40 (К1) | ГОСТ 32414-2013 | | выбор заказчика | м | 1 | | 0,3 + 0,6 + 10 % |
| 23 | Труба канализационная ПП Ø50 (К1) | ГОСТ 32414-2013 | | выбор заказчика | м | 8,5 | | 5,6 + 2,1 + 10 % |
| 24 | Труба канализационная ПП Ø110 (К1) | ГОСТ 32414-2013 | | выбор заказчика | м | 4,5 | | 3,5 + 0,4 + 10 % |
| | Фасонные части и выводы | | | | | | | |
| 25 | Отвод канализационный ПП 45° Ø40 | ГОСТ 32414-2013 | | выбор заказчика | шт | 2 | | 2 шт. на поворот |
| 26 | Отвод канализационный ПП 45° Ø50 | ГОСТ 32414-2013 | | выбор заказчика | шт | 24 | | 2 шт. на поворот |
| 27 | Отвод канализационный ПП 45° Ø110 | ГОСТ 32414-2013 | | выбор заказчика | шт | 12 | | 2 шт. на поворот |
| 28 | Тройник канализационный ПП 45° (врезки ветвей) | ГОСТ 32414-2013 | | выбор заказчика | шт | 8 | | |
| 29 | Ревизия канализационная ПП (после поворота трассы) | ГОСТ 32414-2013 | | выбор заказчика | шт | 11 | | доступ сохранить |
| 30 | Фитинги PP-R Ø20: тройники, угольники 90° (ветви и повороты В1, Т3) | ГОСТ 32415-2013 | | выбор заказчика | шт | 42 | | |
| 31 | Водорозетка PP-R Ø20×½" настенная, с креплением | ГОСТ 32415-2013 | | выбор заказчика | шт | 14 | | коды — лист выводов |
| | Узлы ввода, люки, короба | | | | | | | |
| 32 | Кран шаровой латунный Ду15 PN16 (отключение ввода) | аналог | | выбор заказчика | шт | 8 | | Ст В1-1, Ст Т3-1, Ст В1-2, Ст Т3-2, Ст В1-3*, Ст Т3-3*, Ст В1-4, Ст Т3-4 |
| 33 | Фильтр сетчатый косой Ду15 | аналог | | выбор заказчика | шт | 8 | | |
| 34 | Счётчик воды крыльчатый Ду15 (ХВ, ГВ), с поверкой | аналог | | выбор заказчика | шт | 8 | | пломба УК |
| 35 | Клапан обратный Ду15 | аналог | | выбор заказчика | шт | 8 | | |
| 36 | Люк ревизионный нажимной под плитку 300×400 мм | аналог | | выбор заказчика | шт | 4 | | к стоякам и арматуре |
| 37 | Звукоизоляция стояка К1 в коробе: рулонный звукоизоляционный материал ≥ 10 мм, обмотка стояка на высоту этажа | аналог | | выбор заказчика | м | 10,8 | | Ст К1-1, Ст К1-2 (кухня), Ст К1-3*, Ст К1-4 (постирочная) |
| 38 | Короб К1 над полом: профиль ПН/ПС, ГКЛВ 12,5 мм под плитку | аналог | | выбор заказчика | м | 7,8 | | сечение — лист разводки |

## Примечания

1. Форма 1 ГОСТ 21.110-2013, ширины граф изменены по п. 4.1. «Аналог» — аналог по характеристикам: модели внести до черновых работ, привязки выводов сверить по паспортам.
2. Бытовая техника не входит (показана арматура подключения), мойка — в комплекте кухни (марка — модуля кухни, как у столяра). Длины труб — трасса листа разводки + подъёмы + 10 %.
3. Стояк К1 в коробе — звукоизоляция стояка в коробе без жёсткого контакта короба с трубой. Стояки со «*» (Ст К1-3*, Ст В1-3*, Ст Т3-3*) приняты положение и число узлов ввода сверить на объекте.
4. Расчёт систем водоснабжения и канализации, диаметры магистралей и подбор оборудования выполняет проектная организация.

**Допущения и предложения на листе**

Основа листа: размеры сняты со скана обмерного плана KV оформление (см): часть подписей не читается, помещения выровнены по читаемым размерам; контрольный обмер не выполнен (К-1); высота потолка 2650 мм принята по отметкам обмера (Н = 2,50…2,66 м, ригель 2,28 м) — уточнить при обмере (К-2); толщины стен 300 / 120 мм приняты, межквартирная стена и колонны — по скану, не замерены (К-1); разрешённая мощность 15 кВт принята по типовым ТУ; при объединении двух квартир — переоформление ТУ (К-4); подрайон климата не задан — принят не северный (жилые от 2,5 м) (К-8).

Знак «*» — принято, не замерено и не подтверждено (замерить на объекте): К-6: Ст К1-3, Ст В1-3, Ст Т3-3 — положение снято со скана обмера, отдельно не замерялось; ось внутри габарита поддона См1 — обмер угла по К-6.

См. лист открытых вопросов (лист 6, записи К-1, К-2, К-4, К-6, К-8).

| Изм. | Кол.уч | Лист | № док. | Подп. | Дата |
|---|---|---|---|---|---|
| Разраб. | | Кырлан А.С. | | | 04.11.26 |
| Пров. | | | | | |
| ГИП | | | | | |
| | | | | | |
| Н. контр. | | | | | |
| Утв. | | | | | |

**ГД-2026-009-АИ**

Квартира 103 м²

Общая площадь 100,72* м² · * размеры со скана, не замерены (реестр — л. 6, 7, К-1)

| Дизайн-проект интерьера | Стадия | Лист | Листов |
|---|---|---|---|
| | РП | 42 | 120 |

**Спецификация сантехнического оборудования**

М б/м

**Кырлан Александр Сергеевич**

# Техническое задание на подбор светильников

**ПРЕДВАРИТЕЛЬНО · не для производства работ · открыто пунктов: 8 (реестр — л. 6, 7)**

Параметры для подбора: светильники, ленты и блоки питания, сценарии помещений со светорегуляторами · б/м

## Параметры светильников для подбора

| Поз. | Марки | Наименование | Установка | Кол. | P, Вт | Σ P, Вт | Ф, лм | Тц, К | Ra | Угол, ° | IP | Дим. | Слой | Группа | Пом. |
|---|---|---|---|---|---|---|---|---|---|---|---|---|---|---|---|
| 1 | Св17–Св22, Св56–Св61 | Встраиваемый точечный | в ГКЛ, корпус ≤ 70 мм | 12 | 12 | 144 | 1050 | 2700 | 90 | — | 20 | — | общий | L7, L15 | 1, 8 |
| 2 | Св23**, Св62** | Лента светодиодная 24 В | на поверхности, профиль с рассеивателем | 24,6 м | 9,6/м | 236,2 | 900/м | 2700 | 90 | — | 20 | да | акцентный | L8, L16 | 1, 8 |
| 3 | Св16, Св55 | Потолочный накладной | на потолке, засветка стены | 2 | 10 | 20 | 900 | 3000 | 90 | — | 20 | — | общий | L6, L14 | 2, 7 |
| 4 | Св1–Св8, Св31–Св37 | Встраиваемый точечный | в ГКЛ, корпус ≤ 70 мм | 15 | 12 | 180 | 1000 | 3000 | 90 | — | 20 | — | общий | L1, L4 | 3, 5 |
| 5 | Св9 | Подвесной | подвес, низ H=1600 | 1 | 15 | 15 | 1200 | 2700 | 90 | — | 20 | — | рабочий | L2 | 3 |
| 6 | Св10** | Лента светодиодная 24 В | на поверхности, профиль с рассеивателем | 5,4 м | 9,6/м | 51,8 | 900/м | 2700 | 90 | — | 20 | да | акцентный | L3 | 3 |
| 7 | Св26–Св29, Св53, Св54 | Встраиваемый точечный | в ГКЛ, корпус ≤ 70 мм | 6 | 7 | 42 | 600 | 3000 | 90 | — | 20 | — | общий | L10 | 4, 9 |
| 8 | Св30** | Лента светодиодная 24 В | на поверхности, профиль с рассеивателем, датчик движения | 1,8 м | 4,8/м | 8,6 | 150/м | 2700 | 90 | — | 20 | нет | ночной | L11 | 4 |
| 9 | Св38, Св39 | Линейный светильник | на поверхности | 1,2 м | 8 | 16 | 700 | 3000 | 90 | — | 20 | — | рабочий | L5 | 5 |
| 10 | Св12–Св14, Св51 | Встраиваемый точечный | в ГКЛ, корпус ≤ 70 мм | 4 | 6 | 24 | 500 | 3000 | 90 | — | 44 | — | общий | L12, L17 | 6, 11 |
| 11 | Св15**, Св52** | Настенный светильник над зеркалом, драйвер встроен | над зеркалом, H=1900 | 2 | 8 | 16 | 600 | 3000 | 90 | — | 44 | — | рабочий | L13, L18 | 6, 11 |
| 12 | Св11, Св64, Св74 | Настенный (бра) | на стене, H=1500 | 3 | 6 | 18 | 400 | 2700 | 90 | 60 | 20 | — | рабочий | L19, L22 | 8, 10 |
| 13 | Св65–Св72 | Встраиваемый точечный | в ГКЛ, корпус ≤ 70 мм | 8 | 12 | 96 | 1000 | 2700 | 90 | — | 20 | — | общий | L20 | 10 |
| 14 | Св73** | Лента светодиодная 24 В | на поверхности, профиль с рассеивателем | 15,5 м | 9,6/м | 148,8 | 900/м | 2700 | 90 | — | 20 | да | акцентный | L21 | 10 |
| 15 | Св50 | Встраиваемый точечный | в ГКЛ, корпус ≤ 70 мм | 1 | 7 | 7 | 600 | 3000 | 90 | — | 44 | — | общий | L17 | 11 |
| | | **Итого** | | **54 шт + 48,5 м** | | **1023,4** | | | | | | | | | |

## LED-ленты, линейные светильники и блоки питания

| Марка | Пом. | L, м | U, В | Вт/м | Σ P, Вт | БП | P БП, Вт | Загр., % | Питание | Доступ к БП |
|---|---|---|---|---|---|---|---|---|---|---|
| Св23** | 1 | 12,3 | 24 | 9,6 | 118,1 | БП2 | 200 | 59 | с двух концов | люк 300×300 в коробе У1 у окна |
| Св10** | 3 | 5,4 | 24 | 9,6 | 51,8 | БП1 | 100 | 52 | с одного конца | люк 300×300 в коробе потолка у стены А |
| Св30** | 4 | 1,8 | 24 | 4,8 | 8,6 | БП3 | 20 | 43 | с одного конца | в шкафу П1, верхняя полка |
| Св38 | 5 | 0,6 | 24 | — | 8 | БП4 | 30 | 53 | встроенный ввод | в колонне Кх5 над холодильником, съёмная панель |
| Св39 | 5 | 0,6 | 24 | — | 8 | БП4 | 30 | 53 | встроенный ввод | в колонне Кх5 над холодильником, съёмная панель |
| Св62** | 8 | 12,3 | 24 | 9,6 | 118,1 | БП5 | 200 | 59 | с двух концов | люк 300×300 в коробе У1 у окна |
| Св73** | 10 | 15,5 | 24 | 9,6 | 148,8 | БП6 | 200 | 74 | с двух концов | люк 300×300 в коробе У1 у входа |

## Сценарии (помещения со светорегуляторами)

| Помещение | Сценарий | Горят группы (уровень) | Управление |
|---|---|---|---|
| 3. Гостиная-столовая | Вечер | L2 подвес над обеденным столом — вкл.;<br>L3 лента в карнизе (диммер) — 50 %; остальные выкл. | светорегулятор S2**;<br>выключатель S1 |
| | Гости | L1 общий свет (споты) — вкл.;<br>L2 подвес над обеденным столом — вкл.;<br>L3 лента в карнизе (диммер) — 100 % | светорегулятор S2**;<br>выключатель S1 |
| | Кино | L3 лента в карнизе (диммер) — 20 %; остальные выкл. | светорегулятор S2** |
| | Уборка | L1 общий свет (споты) — вкл.;<br>L2 подвес над обеденным столом — вкл.; остальные выкл. | выключатель S1 |

**Допущения и предложения на листе**

Основа листа: размеры сняты со скана обмерного плана KV оформление (см): часть подписей не читается, помещения выровнены по читаемым размерам; контрольный обмер не выполнен (К-1); высота потолка 2650 мм принята по отметкам обмера (H = 2,50…2,66 м, ригель 2,28 м) — уточнить при обмере (К-2); толщины стен 300 / 120 мм приняты, межквартирная стена и колонны — по скану, не замерены (К-1); разрешённая мощность 15 кВт принята по типовым ТУ; при объединении двух квартир — переоформление ТУ (К-4); подрайон климата не задан — принят не северный (жилые от 2,5 м) (К-8).

Знак «**» — предложение проектировщика, заказчиком не утверждено (согласовать с заказчиком): Св23, Св10, Св30, Св62, Св73 — открытая лента в накладном профиле вместо «в коробе»: короба в потолке нет — высота 2650 мм < 2700 — один уровень (табл. 1.3); S2 — светорегулятор добавлен под диммируемую ленту L3; уровни сценариев выбраны конвейером; Св15 — Сдвиг под раскладку плитки стены Г на 141 мм вдоль стены — ось на шве или в центре плитки, привязка по таблице листа; Св52 — свет у зеркала — над зеркалом у умывальника по его оси (свет на лицо, а не над сантехникой); сдвиг под раскладку плитки стены А на 149 мм вдоль стены — ось на шве или в центре плитки, привязка по таблице листа.

См. лист открытых вопросов (лист 6, записи К-1, К-2, К-4, К-8).

## Примечания

1. Позиции и марки Св — те же, что на плане освещения (лист 24) и в ведомости светильников (лист 26); группы L — по плану выключателей (лист 25).
2. Модели светильников не выбраны: лист — техническое задание на подбор. Модель по строке таблицы: поток, Тц, Ra, угол, IP и регулировка яркости не хуже указанных, мощность не больше; встраиваемые — под глубину короба (графа «Установка»). IP 20 — сухие помещения. После выбора моделей (артикул, производитель) лист выпускается как «Спецификация светильников».
3. Длина LED-ленты в карнизе — по линии карниза плана потолков (лист 45); Σ P = Вт/м × длина. Блок питания загружен не больше чем на 80 %; лента 24 В длиннее 10 м питается с двух концов; доступ к блоку питания — люк ревизии 300×300 мм или место, указанное в таблице.
4. Сценарии: % — яркость группы на светорегуляторе; «вкл.» — группа на обычной клавише; группы, не названные в строке, выключены. Светильники и блоки питания групп на светорегуляторе — с регулировкой яркости. Клавиши и светорегуляторы — лист 25.
5. В пом. 1, 8, 10 свет включается клавишами групп — лист 25.
6. Мощность и поток в таблице — требования к подбору (поток не меньше, мощность не больше указанных); после выбора модели — по её паспорту, Σ P — установленная мощность освещения. Оценка освещённости — на плане освещения; это не светотехнический расчёт.
7. Окончание: «Слои света по помещениям» — лист 44.

| Изм. | Кол.уч | Лист | № док. | Подп. | Дата |
|---|---|---|---|---|---|
| Разраб. | | Кырлан А.С. | | | 04.11.26 |
| Пров. | | | | | |
| ГИП | | | | | |
| | | | | | |
| Н. контр. | | | | | |
| Утв. | | | | | |

**ГД-2026-009-АИ**

Квартира 103 м²

Общая площадь 100,72* м² · * размеры со скана, не замерены (реестр — л. 6, 7, К-1)

Дизайн-проект интерьера

| Стадия | Лист | Листов |
|---|---|---|
| РП | 43 | 120 |

**Техническое задание на подбор светильников**

М б/м

**Кырлан Александр Сергеевич**

выпуск 04.11.2026 № 35b47f1c2a · стр. 48 из 130

# Техническое задание на подбор светильников (продолжение)

Продолжение таблиц · б/м

## Слои света по помещениям

| Пом. | Помещение | Слои света — группы включения (марки — в спецификации) | Σ P, Вт |
|---|---|---|---|
| 1 | Кабинет-библиотека | общий — L7; акцентный — L8 | 190,1 |
| 2 | Кладовая | общий — L6 | 10 |
| 3 | Гостиная-столовая | общий — L1; рабочий — L2; акцентный — L3 | 162,8 |
| 4 | Прихожая-холл | общий — L10; ночной — L11 | 36,6 |
| 5 | Кухня | общий — L4; рабочий — L5 | 100 |
| 6 | Ванная | общий — L12; рабочий — L13 | 26 |
| 7 | Постирочная | общий — L14 | 10 |
| 8 | Спальня 2 | общий — L15; рабочий — L19; акцентный — L16 | 196,1 |
| 9 | Коридор | общий — L10 | 14 |
| 10 | Спальня мастер | общий — L20; рабочий — L22; акцентный — L21 | 256,8 |
| 11 | Ванная мастер | общий — L17; рабочий — L18 | 21 |

## Слои света

общий — равномерный свет помещения, по норме освещённости

рабочий — местный свет задачи: столешница, зеркало, чтение у кровати

акцентный — подсветка потолка, стен и ниш; не входит в поток общего света

ночной — путь спальня → санузел: не выше 2700 K, малая яркость, датчик движения

## Примечания

1. Продолжение листа 43: позиции, марки и группы — те же, что на основном листе.
2. Σ P — установленная мощность освещения помещения, Вт; группы L — по плану выключателей.

**Допущения и предложения на листе**

Основа листа: размеры сняты со скана обмерного плана KV оформление (см): часть подписей не читается, помещения выровнены по читаемым размерам; контрольный обмер не выполнен (К-1); высота потолка 2650 мм принята по отметкам обмера (H = 2,50…2,66 м, ригель 2,28 м) — уточнить при обмере (К-2); толщины стен 300 / 120 мм приняты, межквартирная стена и колонны — по скану, не замерены (К-1); разрешённая мощность 15 кВт принята по типовым ТУ; при объединении двух квартир — переоформление ТУ (К-4); подрайон климата не задан — принят не северный (жилые от 2,5 м) (К-8).

См. лист открытых вопросов (лист 6, записи К-1, К-2, К-4, К-8).

| Изм. | Кол.уч | Лист | № док. | Подп. | Дата |
|---|---|---|---|---|---|
| Разраб. | | Кырлан А.С. | | | 04.11.26 |
| Пров. | | | | | |
| ГИП | | | | | |
| | | | | | |
| Н. контр. | | | | | |
| Утв. | | | | | |

**ГД-2026-009-АИ**

Квартира 103 м²

Общая площадь 100,72* м² · * размеры со скана, не замерены (реестр — л. 6, 7, К-1)

Дизайн-проект интерьера

| Стадия | Лист | Листов |
|---|---|---|
| РП | 44 | 120 |

**Техническое задание на подбор светильников (продолжение)**

М б/м

**Кырлан Александр Сергеевич**

06


# Потолки и ГКЛ-конструкции

Кырлан Александр Сергеевич

выпуск 04.11.2026 · 35b47f1c2a · стр. 50 из 130

# План потолков

Уровни и марки потолков, короба с подсветкой, ниши под шторы, люки, вырезы · отметки низа от ±0,000 чистого пола · размеры в мм

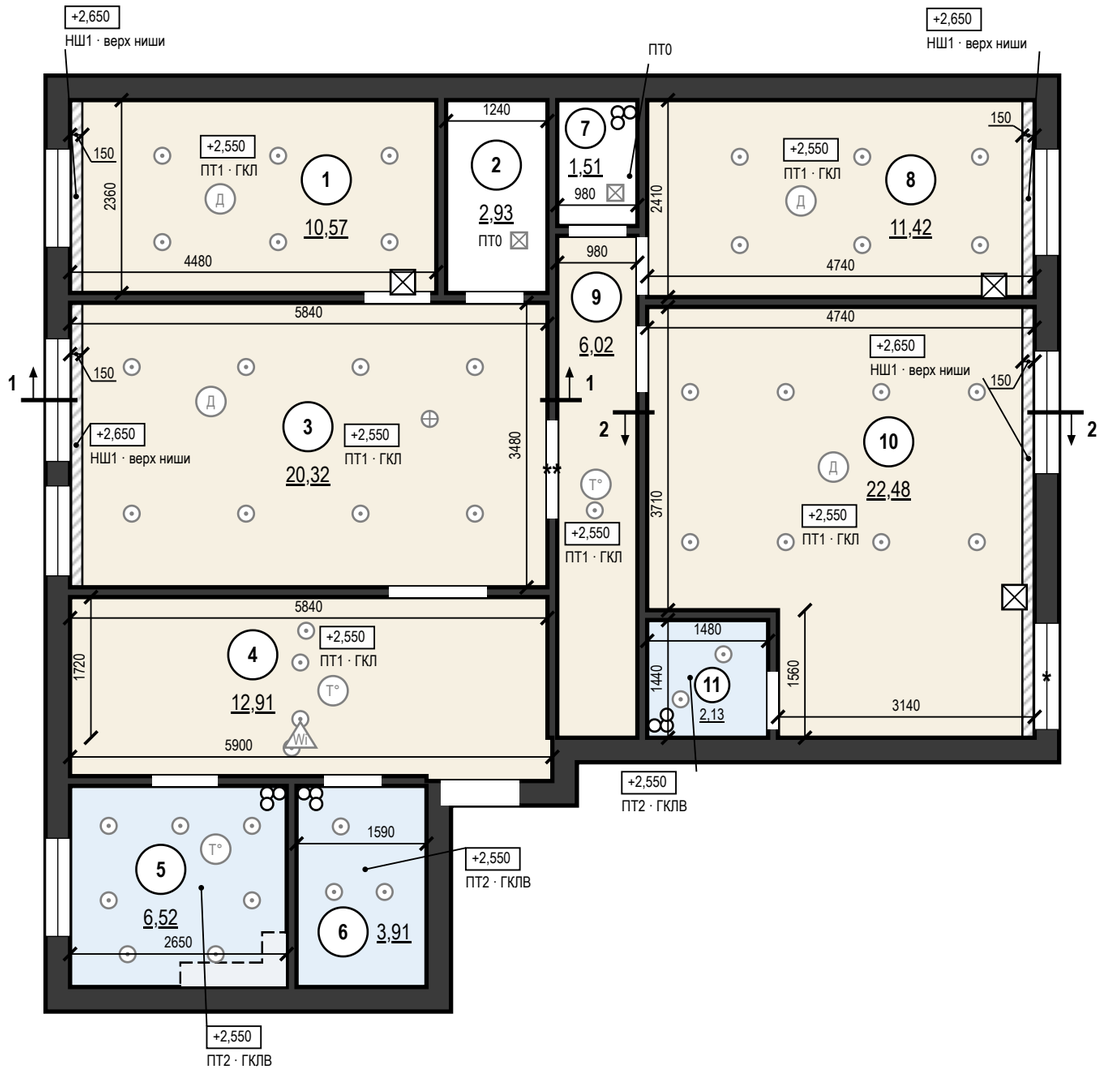


## Условные обозначения

- ПТ1 — ГКЛ по каркасу П113, низ +2,550
- ПТ2 — ГКЛВ по каркасу П113, низ +2,550
- ПТ0 — существующий потолок, окраска, без подвесного потолка, низ +2,650
- НШ1 — ниша под шторы 150×100, верх +2,650
- граница уровней потолка (перепад)
- стояк: К1 — канализация, В1 — ХВС, Т3 — ГВС
- люк ревизии в потолке 300×300 мм (доступ к БП LED)
- светильник встраиваемый — подложка с плана освещения
- светильник накладной — подложка с плана освещения
- светильник подвесной — подложка с плана освещения
- Д — извещатель дымовой на потолке подложка
- Т° — извещатель тепловой на потолке подложка
- Wi — точка доступа Wi-Fi на потолке подложка
- короб воздуховода вытяжки ГКЛ (трасса — план вентиляции)
- линия разреза у стен помещения, стрелка — направление взгляда
- +2,600 — отметка низа потолка, м (у ниши под шторы — верх ниши); под ней марка потолка
- 1 — номер помещения, площадь м²

## Ведомость потолков

| Пом. | Марка | Конструкция | Низ / верх ниши | S, м² | Q |
|---|---|---|---|---|---|
| 1 | ПТ1 | ГКЛ П113 | +2,550 | 10,22 | Q3 |
| 1 | НШ1 | ниша под шторы 150×100 | +2,650 | 0,35 | |
| 2, 7 | ПТ0 | Существующий потолок, окраска | +2,650 | 4,44 | |
| 3 | ПТ1 | ГКЛ П113 | +2,550 | 19,80 | Q3 |
| 3 | НШ1 | ниша под шторы 150×100 | +2,650 | 0,52 | |
| 4 | ПТ1 | ГКЛ П113 | +2,550 | 12,91 | Q3 |
| 5 | ПТ2 | ГКЛВ П113 | +2,550 | 6,52 | Q3 |
| 6 | ПТ2 | То же | +2,550 | 3,91 | Q3 |
| 8 | ПТ1 | ГКЛ П113 | +2,550 | 11,06 | Q3 |
| 8 | НШ1 | ниша под шторы 150×100 | +2,650 | 0,36 | |
| 9 | ПТ1 | ГКЛ П113 | +2,550 | 6,02 | Q3 |
| 10 | ПТ1 | То же | +2,550 | 21,69 | Q3 |
| 10 | НШ1 | ниша под шторы 150×100 | +2,650 | 0,79 | |
| 11 | ПТ2 | ГКЛВ П113 | +2,550 | 2,13 | Q3 |
| | | **Итого** | | **100,72** | |

## Ведомость вырезов и закладных в потолке

| Марка | Устройство | Кол. | Пом. |
|---|---|---|---|
| | Светильник встраиваемый (марки — план освещения) | 46 | 1, 3, 4, 5, 6, 8, 9, 10, 11 |
| | Светильник накладной (марки — план освещения) | 2 | 2, 7 |
| | Светильник подвесной (марки — план освещения) | 1 | 3 |
| ИП2, ИП1, ИП7, ИП8 | Извещатель дымовой | 4 | 1, 3, 8, 10 |
| ИП3, ИП4, ИП6 | Извещатель тепловой | 3 | 4, 5, 9 |
| АР1** | Точка доступа Wi-Fi, PoE | 1 | 4 |
| | Люк ревизии 300×300 | 3 | 1, 8, 10 |

**Допущения и предложения на листе**

Основа листа: размеры сняты со скана обмерного плана KV оформление (см): часть подписей не читается, помещения выровнены по читаемым размерам; контрольный обмер не выполнен (К-1); высота потолка 2650 мм принята по отметкам обмера (Н = 2,50…2,66 м, ригель 2,28 м) — уточнить при обмере (К-2); толщины стен 300 / 120 мм приняты, межквартирная стена и колонны — по скану, не замерены (К-1); разрешённая мощность 15 кВт принята по типовым ТУ; при объединении двух квартир — переоформление ТУ (К-4); подрайон климата не задан — принят не северный (жилые от 2,5 м) (К-8).

Знак «*» — принято, не замерено и не подтверждено (замерить на объекте): К-1: окно пом. 10 (стена Б) — Окно 1300 при смещение 3500 на стене Б основной части (длина 3830) выходило за стену на 970 мм; К-6: Ст К1-3, Ст В1-3, Ст Т3-3 — положение снято со скана обмера, отдельно не замерялось; ось внутри габарита поддона См1 — обмер угла по К-6.

Знак «**» — предложение проектировщика, заказчиком не утверждено (согласовать с заказчиком): АР1 — точка доступа Wi-Fi: число и места; К-5: дверь пом. 3 (стена Б) — проём в межквартирной стене — объединение квартир, предложение до техзаключения.

Открытые вопросы и конфликты по листу: К-2, К-8.

См. лист открытых вопросов (лист 6, записи К-1, К-2, К-4–К-6, К-8).

## Примечания

1. За отметку ±0,000 принят уровень чистого пола сухих помещений (готовое покрытие), а не существующего пола; пол пом. 6, 11 — −0,015; верх плиты перекрытия −0,064 — расчётный по пирогу пола, не замерен; существующий пол снимается до плиты, его отметка не замерена. Отметки в прямоугольниках — низ потолка; низ перекрытия +2,650. Марка потолка — одна конструкция и отметка на весь альбом.
2. Размеры помещений в свету (ширина × длина, мм), не поместившиеся на плане: пом. 2 — 1240 × 2360; пом. 4 — 5840 × 1720, 5900 × 470, 1540 × 60; пом. 5 — 2650 × 2460; пом. 6 — 1590 × 2460; пом. 7 — 980 × 1540; пом. 9 — 980 × 6140.
3. Потолки ГКЛ — каркасная система П113: подвесы через 1000 (с запасом: СП 163, табл. 14 — до 1100 при 0,15 кН/м²), несущие профили через 500, основные через 1200 мм; листы — поперёк несущих профилей. В помещениях 5, 6, 11 — ГКЛВ на оцинкованном каркасе.
4. Ниши под шторы 150×100 мм — на всю длину стены с окном; карниз — на закладной до обшивки (узел 1, лист 46).
5. Примыкание к стенам: теневой шов 15 мм, техзазор 3 мм — пом. 1, 3, 4, 5, 8, 9, 10, по стенам, выровненным штукатуркой (узел 1); пом. 6, 11 — разделительная лента.
6. Светильники и потолочные устройства — подложка с планов освещения, слаботочных систем и вентиляции (положение — по ним); вырезы и закладные — по ведомости на листе, до обшивки; отверстия не совмещать с профилями, глубина корпуса светильника до 70 мм.
7. Разрезы 1–1, 2–2 — на листе 46; высоты мебели и дверных блоков сверены с низом потолка в разрезах.
8. Узлы по выноскам на плане: узел 1 — лист 46; сечения М 1:10 по помещениям — лист 48.
9. Шпаклевание ГКЛ и условия приёмки — Q3: рассеянный дневной свет, осмотр с 2 м; боковой свет не оценивается.
10. Пом. 5: короб воздуховода кухонной вытяжки ГКЛ 300×130 мм (ширина от стены × высота), низ +2,520, длина 1,37 м — по трассе плана вентиляции, вдоль стен до входа в канал; под плоский воздуховод 200×60 (сечение ≈ Ø125): круглый Ø125 в коробе 200 мм опустил бы кухню ниже 2,5 м — сечение подтверждает раздел ОВ; каркас ПН 28×27 по стене и плите, ПП 60×27, лист ГКЛ 12,5.
11. Люки ревизии 300×300 мм — по центру блоков питания LED (БП2, БП5, БП6; координаты — план освещения).
12. Сечения потолков М 1:10: пом. 1 — 1.1, 1.2 (лист 48); пом. 3 — 1.1, 1.2 (лист 48); пом. 8 — 1.1, 1.2 (лист 48); пом. 10 — 1.1, 1.2 (лист 48).

1000 мм · печать 1:1

| Изм. | Кол.уч | Лист | № док. | Подп. | Дата |
|---|---|---|---|---|---|
| Разраб. | | Кырлан А.С. | | | 04.11.26 |
| Пров. | | | | | |
| ГИП | | | | | |
| | | | | | |
| Н. контр. | | | | | |
| Утв. | | | | | |

**ГД-2026-009-АИ**

Квартира 103 м²

Общая площадь 100,72* м² · * размеры со скана, не замерены (реестр — л. 6, 7, К-1)

Дизайн-проект интерьера

| Стадия | Лист | Листов |
|---|---|---|
| РП | 45 | 120 |

**План потолков**

М 1:75

**Кырлан Александр Сергеевич**


выпуск 04.11.2026 № 35b47f1c2a · стр. 51 из 130

# Разрезы и узлы потолков

Разрезы по потолкам с отметками уровней · узлы коробов и ниш · размеры в мм


## Разрез 1–1 (М 1:40)

Пом. 3 Гостиная-столовая; линия разреза — план потолков, лист 45

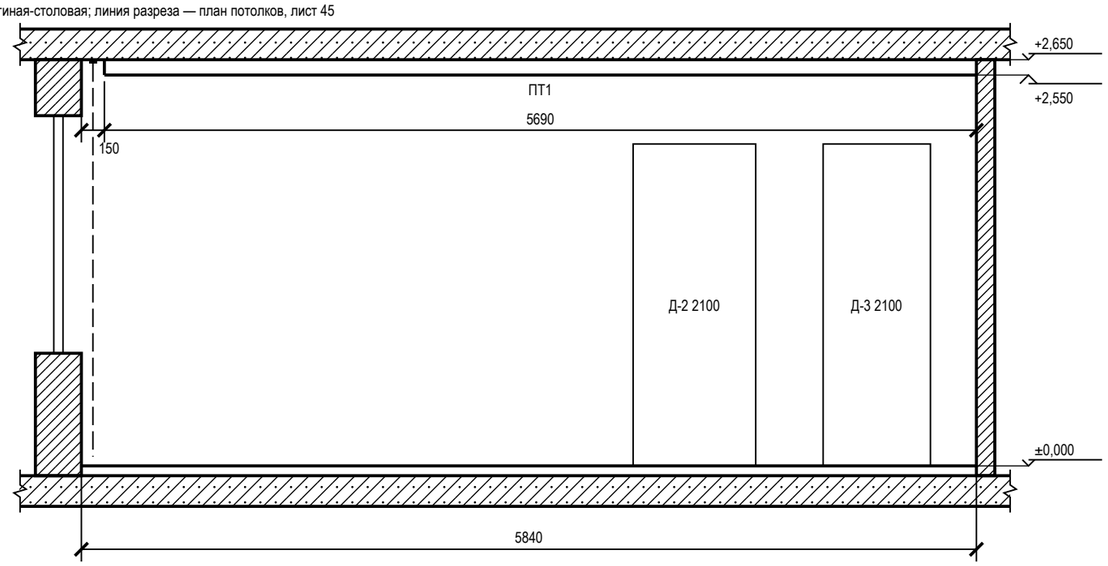



## Разрез 2–2 (М 1:40)

Пом. 10 Спальня мастер; линия разреза — план потолков, лист 45

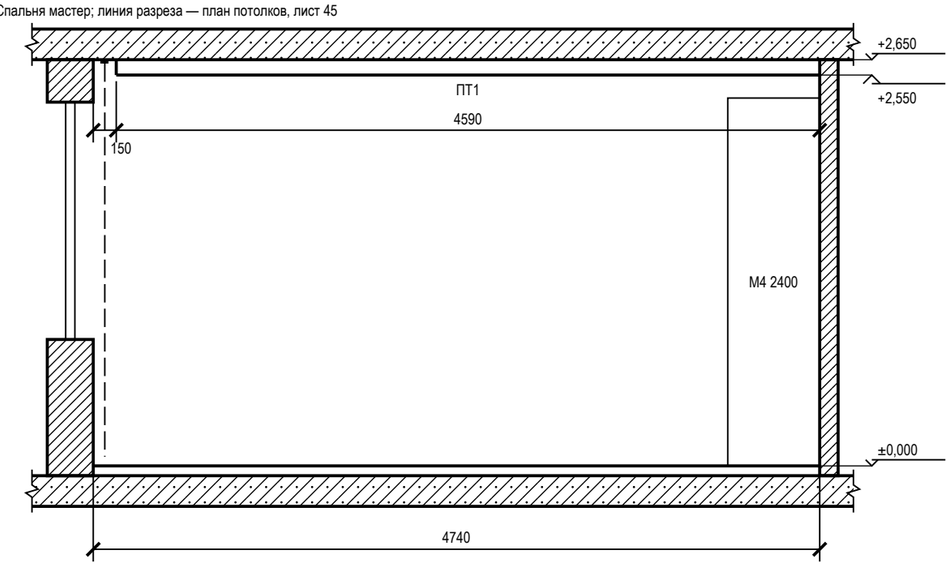


## 1 Ниша под шторы (М 1:10)

Пом. 1, 3, 8, 10; без подсветки; закладные под карниз — до обшивки

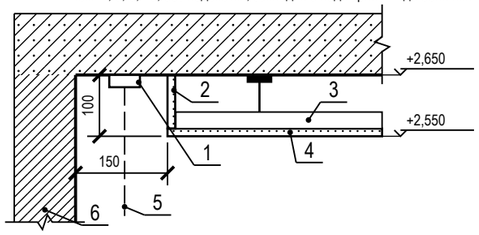


1 — карниз (шина), высота с верхом портьеры 80 мм
2 — стенка ниши — ГКЛ 12,5
3 — ПП 60×27 — каркас короба
4 — низ короба нижнего уровня — ГКЛ 12,5
5 — портьера
6 — стена с окном

## Условные обозначения

- плита перекрытия в сечении
- стена в сечении
- потолок ГКЛ в сечении; под линией — марка потолка (план потолков)
- мебель и дверные проёмы за секущей плоскостью; число — марка и верх от чистого пола, мм
- портьера в нише под шторы

**Допущения и предложения на листе**

Основа листа: размеры сняты со скана обмерного плана KV оформление (см): часть подписей не читается, помещения выровнены по читаемым размерам; контрольный обмер не выполнен (К-1); высота потолка 2650 мм принята по отметкам обмера (Н = 2,50…2,66 м, ригель 2,28 м) — уточнить при обмере (К-2); толщины стен 300 / 120 мм приняты, межквартирная стена и колонны — по скану, не замерены (К-1); разрешённая мощность 15 кВт принята по типовым ТУ; при объединении двух квартир — переоформление ТУ (К-4); подрайон климата не задан — принят не северный (жилые от 2,5 м) (К-8).

См. лист открытых вопросов (лист 6, записи К-1, К-2, К-4, К-8).

## Примечания

1. Разрезы — по линиям 1–1, 2–2 на плане потолков (лист 45). Отметки — от ±0,000 чистого пола, м; размеры — мм.
2. Высоты мебели и дверных блоков за секущей плоскостью сверены с низом потолка над ними: верх ниже низа короба и поля.
3. ГКЛ 12,5 мм по каркасу П113. Ниша под шторы — на всю длину стены с окном, карниз на закладной до обшивки (узел 1 — на этом листе).
4. Толщины плит перекрытия и пирога пола показаны условно.
5. Сечения потолков по помещениям М 1:10 (отметки помещения, профили, подвесы, крепёж, изделия) — лист 48.
6. Ведомость объёмов потолков (лист ГКЛ, профиль, подвесы, лента, блоки питания, люки) — на листе 47.

1000 мм · печать 1:1

| Изм. | Кол.уч | Лист | № док. | Подп. | Дата |
|---|---|---|---|---|---|
| Разраб. | | Кырлан А.С. | | | 04.11.26 |
| Пров. | | | | | |
| ГИП | | | | | |
| | | | | | |
| Н. контр. | | | | | |
| Утв. | | | | | |

**ГД-2026-009-АИ**

Квартира 103 м²

Общая площадь 100,72* м² · * размеры со скана, не замерены (реестр — л. 6, 7, К-1)

Дизайн-проект интерьера

| Стадия | Лист | Листов |
|---|---|---|
| РП | 46 | 120 |

**Разрезы и узлы потолков**

М 1:40; 1:10

**Кырлан Александр Сергеевич**

выпуск 04.11.2026 № 35b47f1c2a · стр. 52 из 130

# Разрезы и узлы потолков (продолжение)

Ведомость объёмов · размеры в мм

**ПРЕДВАРИТЕЛЬНО · не для производства работ · открыто пунктов: 8 (реестр — л. 6, 7)**

### Ведомость объёмов потолков

| Позиция | Ед. | Кол. | Пом. |
|---|---|---|---|
| Лист ГКЛ 12,5 | м² | 85,08 | 1, 3, 4, 8, 9, 10 |
| Лист ГКЛВ 12,5 | м² | 12,56 | 5, 6, 11 |
| Борта и карнизы (входят в площади листов выше) | м² | 1,36 | 1, 3, 8, 10 |
| Профиль ПП 60×27 | м | 276,03 | 1, 3, 4, 5, 6, 8, 9, 10, 11 |
| Профиль ПН 28×27 | м | 148,38 | 1, 3, 4, 5, 6, 8, 9, 10, 11 |
| Подвес прямой | шт. | 84 | 1, 3, 4, 5, 6, 8, 9, 10, 11 |
| Анкер-клин к плите | шт. | 84 | 1, 3, 4, 5, 6, 8, 9, 10, 11 |
| Шуруп TN 3,5×25 | шт. | 2246 | 1, 3, 4, 5, 6, 8, 9, 10, 11 |
| Лента армирующая для швов | м | 117,17 | 1, 3, 4, 5, 6, 8, 9, 10, 11 |
| Шпаклёвка для швов | кг | 39,06 | 1, 3, 4, 5, 6, 8, 9, 10, 11 |
| Грунтовка (швы) | л | 9,76 | 1, 3, 4, 5, 6, 8, 9, 10, 11 |
| Лента разделительная по периметру | м | 121,34 | 1, 3, 4, 5, 6, 8, 9, 10, 11 |
| Сплошная шпаклёвка и окраска (площадь развёртки) | м² | 97,64 | 1, 3, 4, 5, 6, 8, 9, 10, 11 |
| Люк ревизии | шт. | 3 | 1, 8, 10 |

**Допущения и предложения на листе**

Основа листа: размеры сняты со скана обмерного плана KV оформление (см): часть подписей не читается, помещения выровнены по читаемым размерам; контрольный обмер не выполнен (К-1); высота потолка 2650 мм принята по отметкам обмера (Н = 2,50…2,66 м, ригель 2,28 м) — уточнить при обмере (К-2); толщины стен 300 / 120 мм приняты, межквартирная стена и колонны — по скану, не замерены (К-1); разрешённая мощность 15 кВт принята по типовым ТУ; при объединении двух квартир — переоформление ТУ (К-4); подрайон климата не задан — принят не северный (жилые от 2,5 м) (К-8).

См. лист открытых вопросов (лист 6, записи К-1, К-2, К-4, К-8).

### Примечания

1. ГКЛ 12,5 мм по каркасу П113; узлы коробов и ниш под шторы: узел 1 — лист 46; условные обозначения разрезов — на листе 46.
2. Ведомость объёмов — по геометрии плана потолков: Лист ГКЛ 12,5 — плоскости уровней + борта (без арочных участков); Лист ГКЛВ 12,5 — плоскости уровней + борта; Борта и карнизы — длина перепада × перепад; Профиль ПП 60×27 — S × (1/шаг несущ. + 1/шаг осн.) + стойки бортов; Профиль ПН 28×27 — периметр стен + 2 × перепады + карнизы; Подвес прямой — по раскладке: S уровня / (шаг осн. × шаг подвесов), пояс уже шага — ряд вдоль пояса, фигура — по контуру; шаг подвесов — не больше табл. 14 СП 163; Анкер-клин к плите — по одному на подвес (Knauf П113); Шуруп TN 3,5×25 — 23 шт./м² (Knauf П113, табл. 2 альбома П 11); Лента армирующая для швов — 1,2 м/м² листа (Knauf); Шпаклёвка для швов — 0,4 кг/м² листа, только швы (Knauf); Грунтовка (швы) — 0,1 л/м² листа, только швы (Knauf); Лента разделительная по периметру — периметр стен под потолком ГКЛ; Сплошная шпаклёвка и окраска (площадь развёртки) — плоскости + борта; расход — по паспорту материала (норма расхода на сплошной слой не подтверждена); Люк ревизии — план потолков; без запаса на подрезку (при закупке листа: ×1,075 при S > 20 м², ×1,175 — 10–20 м², ×1,275 — < 10 м²).

| | | | | | |
|---|---|---|---|---|---|
| | | | | | |
| | | | | | |
| | | | | | |
| | | | | | |
| Изм. | Кол.уч | Лист | № док. | Подп. | Дата |
| Разраб. | | Кырлан А.С. | | | 04.11.26 |
| Пров. | | | | | |
| ГИП | | | | | |
| | | | | | |
| Н. контр. | | | | | |
| Утв. | | | | | |

**ГД-2026-009-АИ**

Квартира 103 м²

Общая площадь 100,72* м² · * размеры со скана, не замерены (реестр — л. 6, 7, К-1)

Дизайн-проект интерьера

| Стадия | Лист | Листов |
|---|---|---|
| РП | 47 | 120 |

**Разрезы и узлы потолков (продолжение)**

М б/м

**Кырлан Александр Сергеевич**

выпуск 04.11.2026 № 35b47f1c2a · стр. 53 из 130


# Сечения потолков М 1:10

Пом. 1, 3, 8, 10 · профили, подвесы, крепёж, изделия · размеры в мм

**ПРЕДВАРИТЕЛЬНО · не для производства работ · открыто пунктов: 8 (реестр — л. 6, 7)**

### Сечение 1.1. Ниша под шторы (М 1:10)

Пом. 1 Кабинет-библиотека, 3 Гостиная-столовая, 8 Спальня 2, 10 Спальня мастер; без подсветки; закладные под карниз — до обшивки

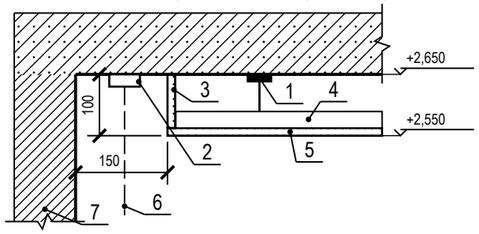


1 — анкер-клин к плите — по одному на подвес; подвес прямой, шаг 1000 мм

2 — карниз (шина), высота с верхом портьеры 80 мм

3 — стенка ниши — ГКЛ 12,5

4 — ПП 60×27 — каркас короба, основные через 1200 мм; соединители одноуровневые, шурупы LN 3,5×9


5 — низ короба нижнего уровня — ГКЛ 12,5; шурупы TN 3,5×25 через 170 мм

6 — портьера

7 — стена с окном

### Сечение 1.2. Примыкание потолка к стене (М 1:10)

Пом. 1 Кабинет-библиотека, 3 Гостиная-столовая, 8 Спальня 2, 10 Спальня мастер; примыкание — теневой шов

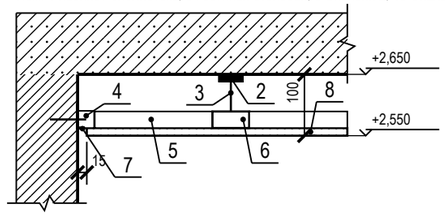


1 — плита перекрытия

2 — анкер-клин к плите — по одному на подвес

3 — подвес прямой, шаг 1000 мм

4 — ПН 28×27 по периметру — дюбель-гвоздь через ≤ 500 мм, не менее 3 на профиль

5 — ПП 60×27 несущий (вид) через 500 мм, в ПН

6 — ПП 60×27 основной (сечение) через 1200 мм; соединители одноуровневые, шурупы LN 3,5×9

7 — теневой профиль: шов 15 мм, зазор 3 мм; стена под шов выровнена

8 — ГКЛ 12,5 по П113; шурупы TN 3,5×25 через 170 мм

**Допущения и предложения на листе**

Основа листа: размеры сняты со скана обмерного плана KV оформление (см): часть подписей не читается, помещения выровнены по читаемым размерам; контрольный обмер не выполнен (К-1); высота потолка 2650 мм принята по отметкам обмера (Н = 2,50…2,66 м, ригель 2,28 м) — уточнить при обмере (К-2); толщины стен 300 / 120 мм приняты, межквартирная стена и колонны — по скану, не замерены (К-1); разрешённая мощность 15 кВт принята по типовым ТУ; при объединении двух квартир — переоформление ТУ (К-4); подрайон климата не задан — принят не северный (жилые от 2,5 м) (К-8).

См. лист открытых вопросов (лист 6, записи К-1, К-2, К-4, К-8).

## Примечания

1. Сечения потолков М 1:10 по помещениям с нишами LED и нишами под шторы: отметки и размеры этого помещения от ±0,000 чистого пола (м, мм). Положение — по плану потолков (лист 45): короб и ниша LED — по линиям ленты, ниша под шторы — у стены с окном; типовые узлы по группам помещений — на листе 46.
2. Крепёж: подвес прямой к плите на анкер-клине — по одному на подвес (Knauf П113); ПН к стенам — дюбель-гвоздь через ≤ 500 мм, не менее 3 на профиль (серия 1.045.9-2.08); лист 12,5 — шурупы TN 3,5×25 через 170 мм (СП 163, табл. 15); профили между собой — соединители одноуровневые, шурупы LN 3,5×9.
3. Изделие карниза, профиля LED и галтели подписано артикулом из данных; где артикул не выбран, сечение дано по габаритам из данных (ширина и глубина ниши, щель под свет), изделие подбирается по ним.

1000 мм · печать 1:1

| Изм. | Кол.уч | Лист | № док. | Подп. | Дата |
|---|---|---|---|---|---|
| Разраб. | | Кырлан А.С. | | | 04.11.26 |
| Пров. | | | | | |
| ГИП | | | | | |
| Н. контр. | | | | | |
| Утв. | | | | | |

**ГД-2026-009-АИ**

Квартира 103 м²

Общая площадь 100,72* м² · * размеры со скана, не замерены (реестр — л. 6, 7, К-1)

Дизайн-проект интерьера

| Стадия | Лист | Листов |
|---|---|---|
| РП | 48 | 120 |

**Сечения потолков М 1:10**

М 1:10


**Кырлан Александр Сергеевич**

выпуск 04.11.2026 № 35b47f1c2a · стр. 54 из 130


# Раскладка плитки. Планы полов

Раскладка от чистовых размеров · размеры в мм · отметки ±0,000

**Фрагмент 1. Ванная (пом. 6). Пол 600×600, шов 2 мм, М 1:25**

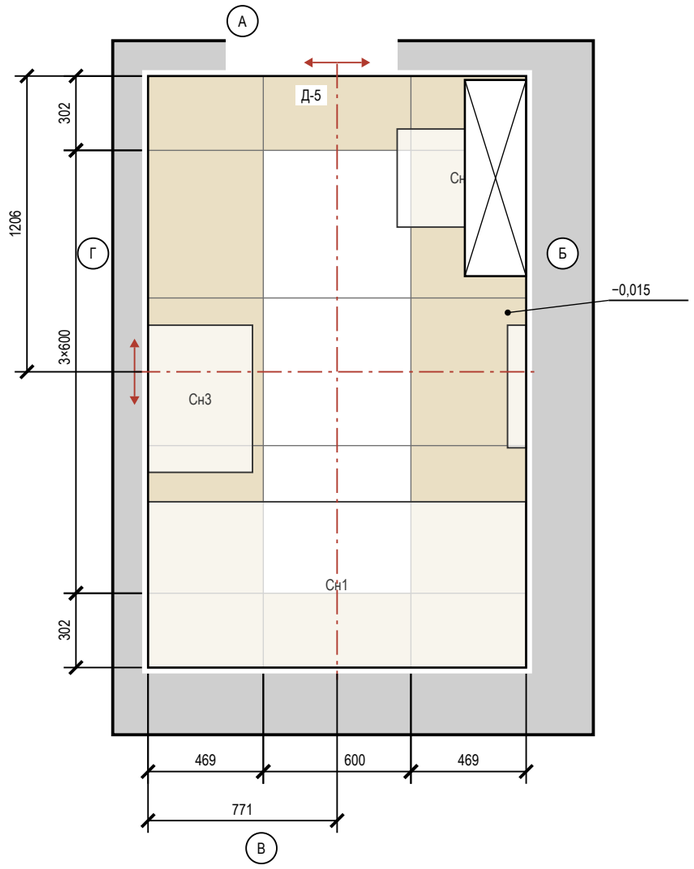


**Фрагмент 2. Ванная мастер (пом. 11). Пол 600×600, шов 2 мм, М 1:25**

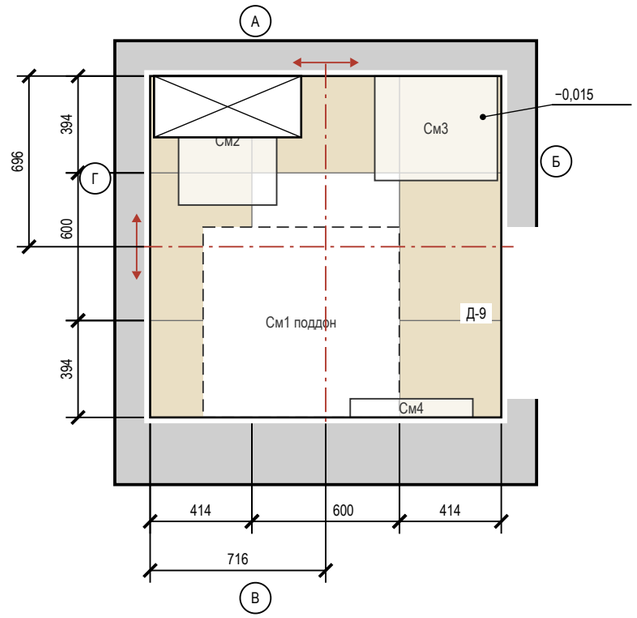


## Ведомость материалов

| Материал | Класс, код | Норма расхода | Кол-во |
|---|---|---|---|
| Затирка | CG2WA Mapei Ultracolor Plus 132 | (a+b)/ab·шов·t·1,6 | 3,0 кг |
| Затирка | CG2WA | (a+b)/ab·шов·t·1,6 | 1,0 кг |
| Клей | C2 TE S1 Ceresit CM 17 | 1,5 кг/м²·мм, слой 5 | 297 кг (12 меш.) |
| Клей | C2 TE S1 | 1,5 кг/м²·мм, слой 5 | 105 кг (5 меш.) |
| Гидроизоляция | обмазочная, 2 слоя: пол, стены по периметру и зоны замачивания | по ТУ | 18,7 м² |
| Демпф. лента | по периметру пола из плитки | | 27,1 м |

**Допущения и предложения на листе**

Основа листа: размеры сняты со скана обмерного плана KV оформление (см): часть подписей не читается, помещения выровнены по читаемым размерам; контрольный обмер не выполнен (К-1); высота потолка 2650 мм принята по отметкам обмера (Н = 2,50…2,66 м, ригель 2,28 м) — уточнить при обмере (К-2); толщины стен 300 / 120 мм приняты, межквартирная стена и колонны — по скану, не замерены (К-1); разрешённая мощность 15 кВт принята по типовым ТУ; при объединении двух квартир — переоформление ТУ (К-4); подрайон климата не задан — принят не северный (жилые от 2,5 м) (К-8).

Знак «**» — предложение проектировщика, заказчиком не утверждено (согласовать с заказчиком): пол пом. 6, 11 — пирог пола: стяжка 33 мм и обмазочная гидроизоляция добавлены разработчиком проекта; артикул изделия не выбран: позиция описана характеристиками («аналог по характеристикам»), артикул выбирается при закупке.

См. лист открытых вопросов (лист 6, записи К-1, К-2, К-4, К-8).

## Ведомость плитки

| Помещение, поверхность | Плитка, код | Формат | Шов | S, м² | Целых | Подр. | С запасом |
|---|---|---|---|---|---|---|---|
| Ванная, пол | Atlas Concorde Marvel Travertine Sand Cross 60×60 Matte Sensitech, арт. AFUL (той же коллекции, что стены A8UZ; тон сверить по образцу) | 600×600 | 2 | 3,91 | 3 | 12 | 17 |
| Ванная, стены А–Г | A8UZ | 600×1200 | 2 | 17,04 | 13 | 19 | 36 |
| Ванная, короб инсталляции | A8UZ | 600×1200 | 2 | 1,76 | 0 | 6 | 7 |
| Ванная мастер, пол | Atlas Concorde Marvel Travertine Sand Cross 60×60 Matte Sensitech, арт. AFUL (той же коллекции, что стены A8UZ; тон сверить по образцу) | 600×600 | 2 | 2,13 | 0 | 8 | 9 |
| Ванная мастер, стены А–Г | A8UZ | 600×1200 | 2 | 11,85 | 5 | 19 | 28 |
| Ванная мастер, короб инсталляции | A8UZ | 600×1200 | 2 | 1,47 | 1 | 3 | 5 |
| Прихожая-холл, пол | A8UZ | 600×1200 | 2 | 12,91 | 0 | 20 | 22 |
| Итого 600×600 | | | | 6,04 | 3 | 20 | 26 |
| **Итого 600×1200** | | | | **45,03** | **19** | **67** | **98** |

## Условные обозначения

- плитка целая; тонкая линия — шов
- плитка с подрезкой (размер — на цепочке)
- ось старта; стрелки — направление укладки
- сантехприбор: габарит, высота по практике
- поддон душа — плитку пола под ним не кладут
- короб инсталляции: плитка пола — до короба
- отметка чистого пола на полке выноски, м
- (А) обозначение стены А–Г (как на развёртках)

## Примечания

1. Раскладка от чистовых размеров: стены санузлов теряют 10 + 5 + 9 = 24 мм на сторону (штукатурка, клей, плитка); подрезки — чистые, без шва.
2. Старт — от центра помещения (штрихпунктир, стрелки — направление укладки); размер старта — от чистовых стен Г и А.
3. Раскладка пола «Прихожая-холл» — на листе «Раскладка плитки. Прихожая-холл».
4. Калибр партии не задан — до укладки замерить (рабочий размер W, ГОСТ 13996-2019) и пересчитать подрезки.
5. Количество: целые по раскладке + по одной на подрезку, запас 10 %; один артикул — одна партия и тон. Исключены поддон, короб, проёмы и места за коробом; S — по чистым граням: стены нетто = зона облицовки по ведомости отделки − место за коробом инсталляции 1,68 м² (плитку за коробом не кладут), короб — отдельной строкой.
6. Клей C2 TE S1 Ceresit CM 17; C2 TE S1 (ГОСТ Р 56387-2018), затирка CG2WA Mapei Ultracolor Plus 132; CG2WA; расход — по ТУ выбранной марки.
7. Гидроизоляция: пол и стены 200 мм от ЧП; над ванной — до 2000 и 300 мм за борт (пом. 6), у душа — до 2000 и 500 мм за поддон (пом. 11) (см. развёртки); акт скрытых работ, пролив 24 ч.
8. Швы пола совмещены со швами стены А; по периметру — демпферная лента.
9. Отметка чистого пола −0,015, порог 15 мм; стык с соседним покрытием — по оси полотна двери.

1000 мм · печать 1:1

| Изм. | Кол.уч | Лист | № док. | Подп. | Дата |
|---|---|---|---|---|---|
| Разраб. | | Кырлан А.С. | | | 04.11.26 |
| Пров. | | | | | |
| ГИП | | | | | |
| Н. контр. | | | | | |
| Утв. | | | | | |

**ГД-2026-009-АИ**

Квартира 103 м²

Общая площадь 100,72* м² · * размеры со скана, не замерены (реестр — л. 6, 7, К-1)

Дизайн-проект интерьера

| Стадия | Лист | Листов |
|---|---|---|
| РП | 49 | 120 |

**Раскладка плитки. Планы полов**


М 1:25

**Кырлан Александр Сергеевич**

# Раскладка плитки. Прихожая-холл

Раскладка от чистовых размеров · размеры в мм · высоты фартука от чистого пола

**Фрагмент 1. Прихожая-холл (пом. 4). Пол 600×1200, шов 2 мм, М 1:20**

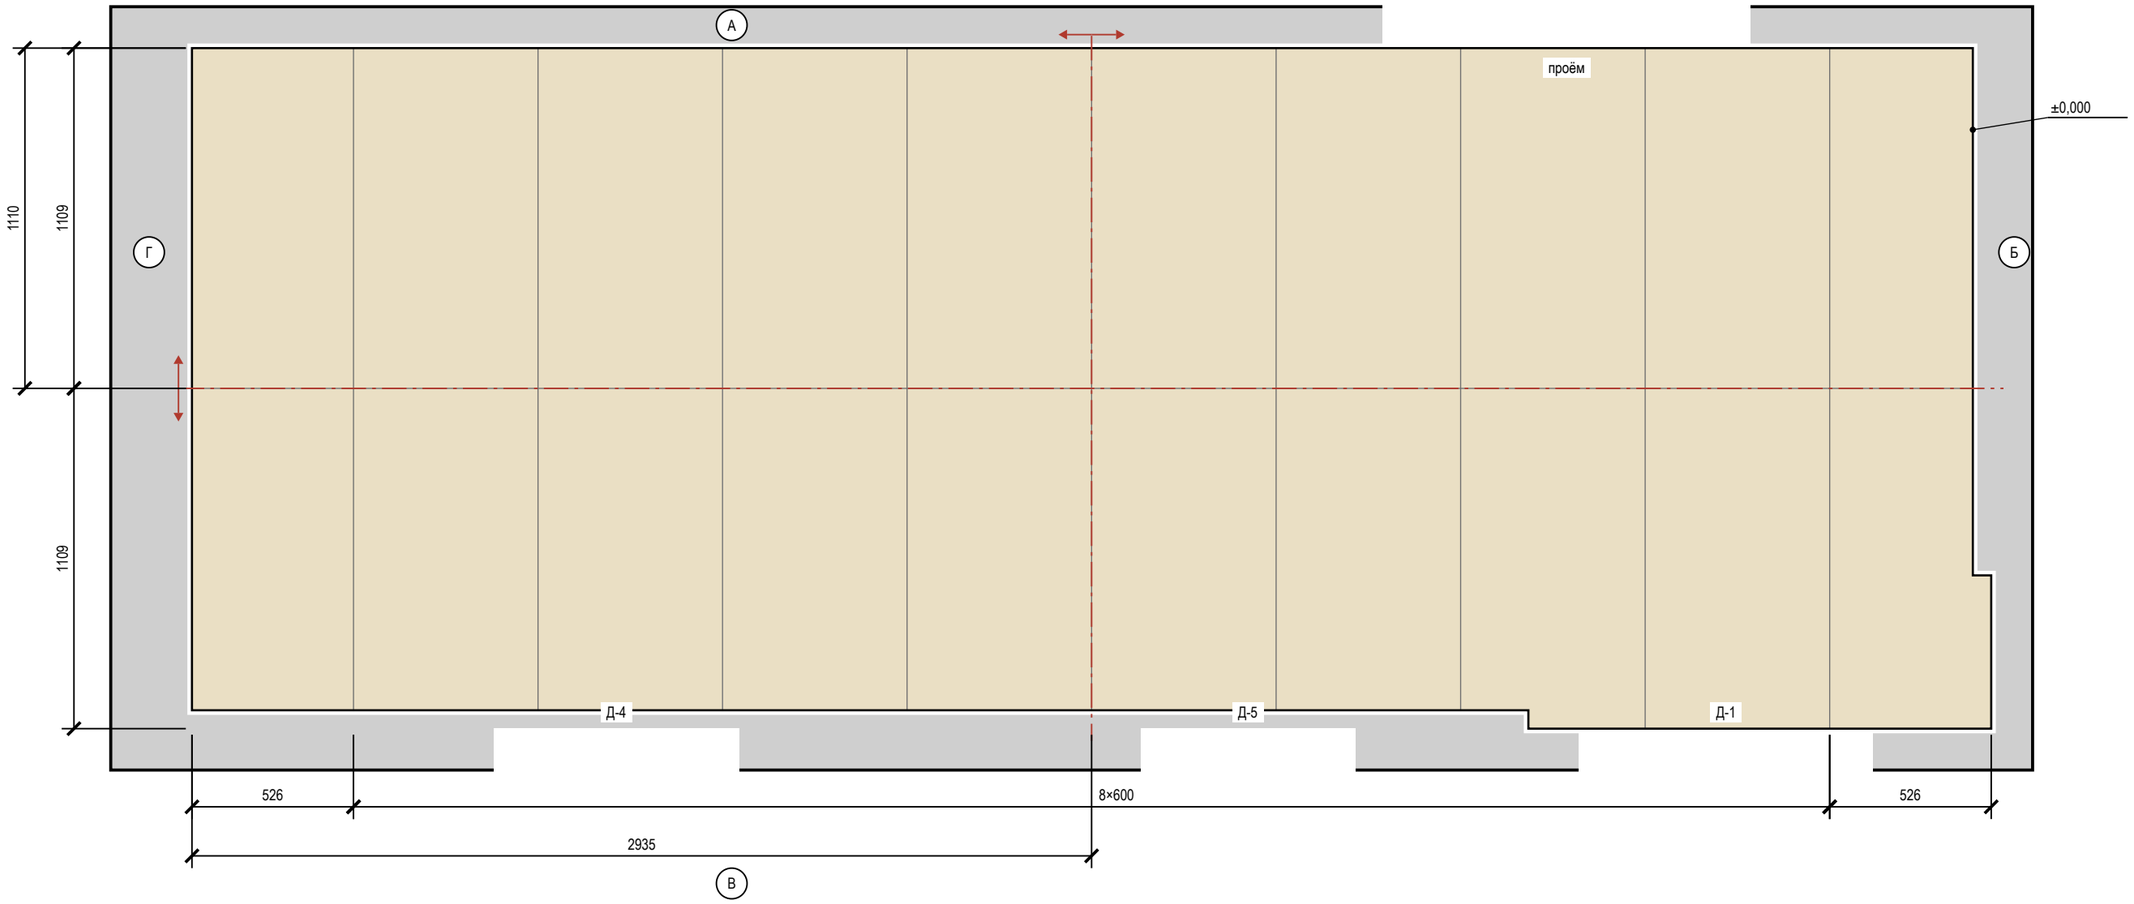


## Условные обозначения

- плитка целая; тонкая линия — шов
- плитка с подрезкой (размер — на цепочке)
- ось старта; стрелки — направление укладки
- отметка чистого пола на полке выноски, м
- (А) обозначение стены А–Г (как на развёртках)

## Подсчёт плитки

| Поверхность | Формат | S, м² | Целых | Подр. | С запасом |
|---|---|---|---|---|---|
| Прихожая-холл, пол | 600×1200 | 12,91 | 0 | 20 | 22 |

## Примечания

1. Прихожая-холл: керамогранит 600×1200, длинная сторона — вдоль стен Б и Г, шов 2 мм, прямая раскладка от центра. Стены окрашены: раскладка от чистового контура минус штукатурка и шпаклёвка 15 мм на сторону (принято); подрезки 526 / 1109 мм, срез — под плинтус.
2. Прихожая-холл: деформационный зазор по периметру 8–10 мм под плинтусом; в проёмах — стык с соседним покрытием по оси полотна двери. Клей C2 TE S1, затирка CG2WA.
3. Клей, затирка и итог по форматам — в ведомостях листа «Раскладка плитки. Планы полов».

**Допущения и предложения на листе**

Основа листа: размеры сняты со скана обмерного плана KV оформление (см): часть подписей не читается, помещения выровнены по читаемым размерам; контрольный обмер не выполнен (К-1); высота потолка 2650 мм принята по отметкам обмера (Н = 2,50…2,66 м, ригель 2,28 м) — уточнить при обмере (К-2); толщины стен 300 / 120 мм приняты, межквартирная стена и колонны — по скану, не замерены (К-1); разрешённая мощность 15 кВт принята по типовым ТУ; при объединении двух квартир — переоформление ТУ (К-4); подрайон климата не задан — принят не северный (жилые от 2,5 м) (К-8).

Знак «**» — предложение проектировщика, заказчиком не утверждено (согласовать с заказчиком): плинтус пом. 4 — артикул изделия не выбран: позиция описана характеристиками («аналог по характеристикам»), артикул выбирается при закупке.

См. лист открытых вопросов (лист 6, записи К-1, К-2, К-4, К-8).

1000 мм · печать 1:1

| Изм. | Кол.уч | Лист | № док. | Подп. | Дата |
|---|---|---|---|---|---|
| Разраб. | | Кырлан А.С. | | | 04.11.26 |
| Пров. | | | | | |
| ГИП | | | | | |
| | | | | | |
| Н. контр. | | | | | |
| Утв. | | | | | |

**ГД-2026-009-АИ**

Квартира 103 м²

Общая площадь 100,72* м² · * размеры со скана, не замерены (реестр — л. 6, 7, К-1)

Дизайн-проект интерьера

| Стадия | Лист | Листов |
|---|---|---|
| РП | 50 | 120 |

**Раскладка плитки. Прихожая-холл**


М 1:20

**Кырлан Александр Сергеевич**

# Раскладка плитки. Ванная. Развёртки стен

**ПРЕДВАРИТЕЛЬНО · не для производства работ · открыто пунктов: 8 (реестр — л. 6, 7)**

Пом. 6 · вид изнутри помещения · размеры в мм · высоты от чистого пола, отметки от ±0,000

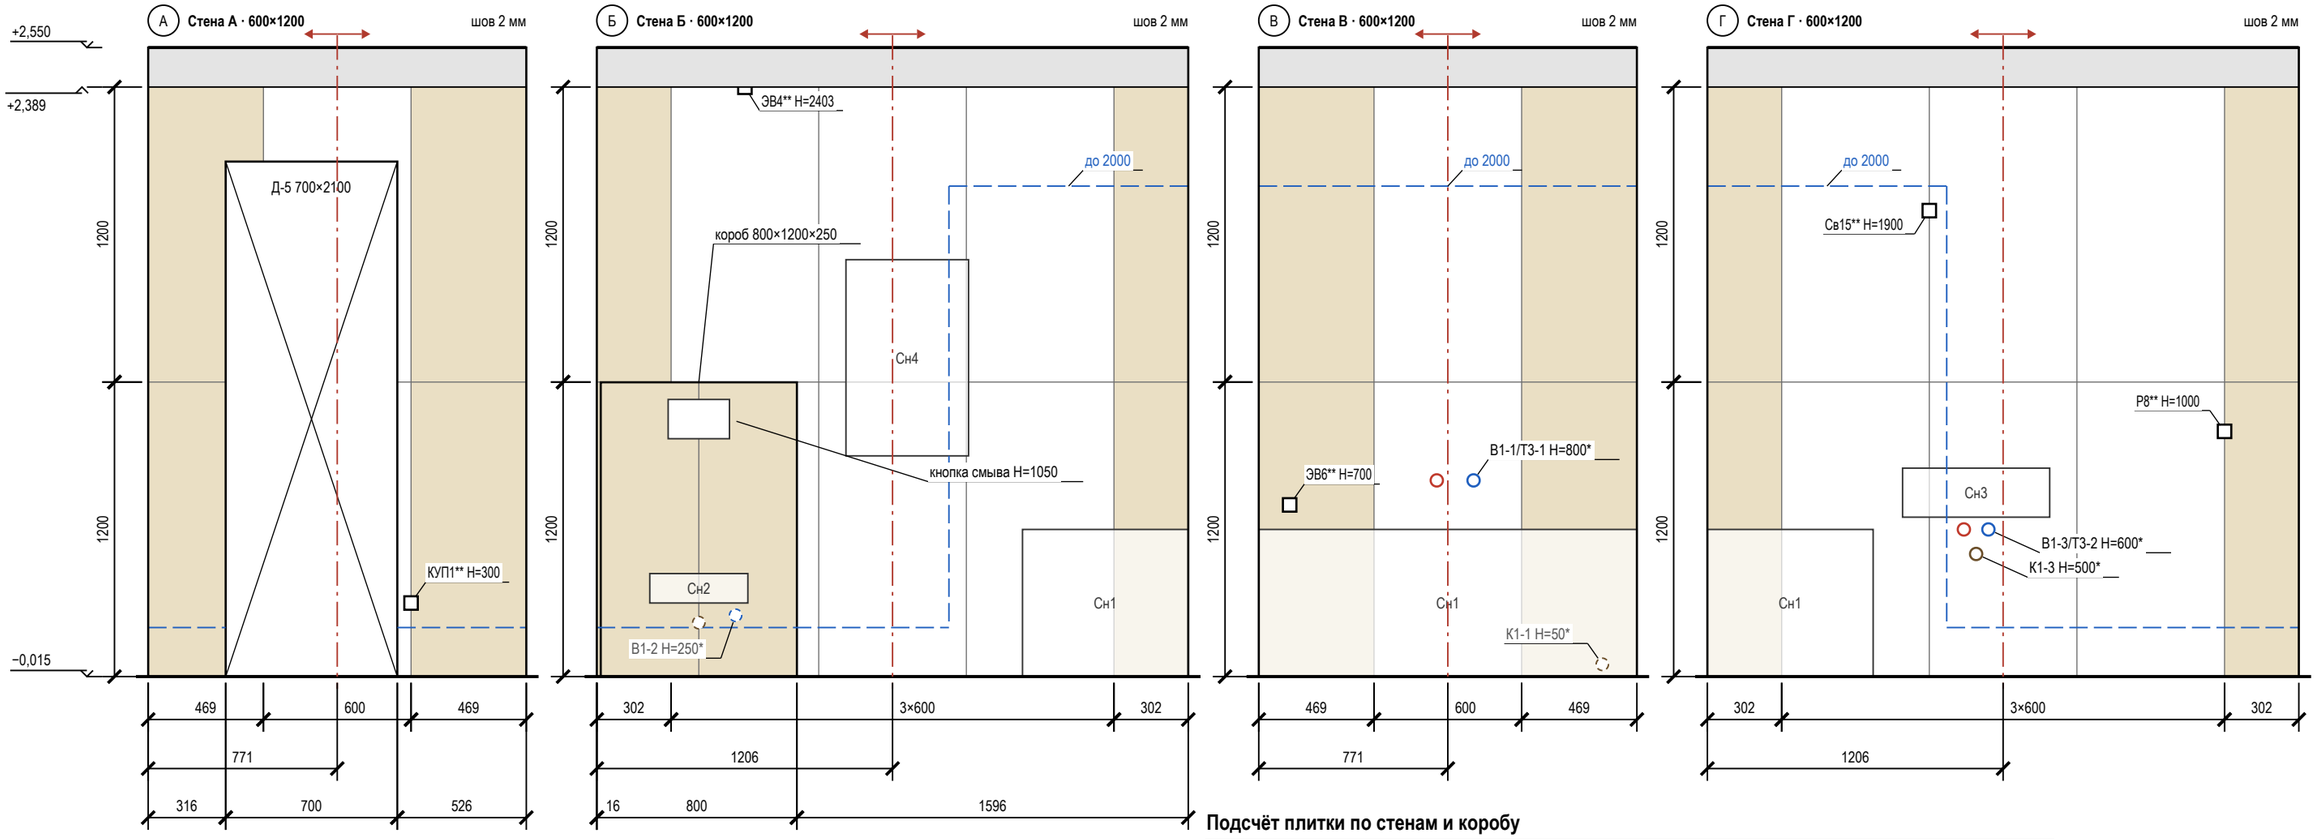


## Подсчёт плитки по стенам и коробу

| Поверхность | L × H, мм | S, м² | Целых | Подр. | С запасом | Подрезки: край / верх, мм |
|---|---|---|---|---|---|---|
| стена А | 1542 × 2404 | 2,35 | 0 | 6 | 7 | 469 / 469; целый ряд |
| стена Б | 2412 × 2404 | 4,95 | 5 | 5 | 11 | 302 / 302; целый ряд |
| короб (ст. Б) | 800×1200×250 | 1,76 | 0 | 6 | 7 | лицо 399 / 399; бок. 250 |
| стена В | 1542 × 2404 | 3,82 | 2 | 4 | 7 | 469 / 469; целый ряд |
| стена Г | 2412 × 2404 | 5,91 | 6 | 4 | 11 | 302 / 302; целый ряд |
| **Итого** | | **18,80** | **13** | **25** | **43** | |

## Сдвиг точек под раскладку

| Точка (ВК, ЭОМ) | Стена | Проект: от угла / H | Под раскладку: от угла / H | Сдвиг, мм |
|---|---|---|---|---|
| ЭВ6** | В | 126 / 700 | 169 / 700 | +43 в центр плитки |

## Условные обозначения

- плитка целая; тонкая линия — шов
- плитка с подрезкой (размер — на цепочке)
- ось старта; стрелки — направление укладки
- верх гидроизоляции: 200 от ЧП, в мокрой зоне — «до …»
- проём — не облицовывается
- сантехприбор: габарит, высота по практике
- короб инсталляции, в нём кнопка смыва 250×160
- вывод В1 (код — в ведомости привязок)
- вывод Т3 (код — в ведомости привязок)
- вывод К1 (код — в ведомости привязок)
- вывод за прибором / в коробе (не на сетке)
- электроточка: марка и H — по листам ЭОМ
- отметка уровня, м: ±0,000 — чистый пол жилых помещений
- низ потолка; серая полоса — стена без плитки
- (А) обозначение стены А–Г (как на развёртках)

1000 мм · печать 1:1

## Примечания

1. Вид изнутри, стены по часовой стрелке А → Г. Высоты — от чистого пола (−0,015), отметки — от ±0,000. Раскладка от чистовых размеров (штукатурка 10 + клей 5 + плитка 9 мм), подрезки чистые; старт — от оси стены, ряды от пола целыми.
2. Верх плитки +2,389, потолок +2,550, зазор 161 мм: потолок ГКЛ опустить до +2,392 (шов 3 мм, герметик) — согласовать с монтажником ГКЛ; иначе профиль-окантовка, полосу окрасить в цвет потолка. Подрезной ряд 156 мм не делать.
3. Точки из таблицы сдвигов переносятся до черновой разводки (ЭОМ — по тем же числам).
4. Выводы ВК стоят по оси прибора и с прибором не двигаются — привязки по «Плану выводов сантехники» без сдвига; вне сетки (В1-1/Т3-1, В1-3/Т3-2, К1-3) отверстие в плитке коронкой по той же привязке, плитку не сдвигать.
5. Выводы — по «Плану выводов сантехники», электроточки — по ЭОМ, «*» — высота по практике; за приборами и в коробе (В1-2, К1-2, К1-1) — штриховым кольцом.
6. Гидроизоляция: 200 мм от ЧП по периметру; над ванной — до 2000 и 300 мм за борт (СП 29.13330.2011, п. 7.2 — на высоту замачивания); углы — лентой; акт скрытых работ, пролив.
7. Короб 800×1200×250: лицо 399 / 399 мм от оси кнопки смыва, боковины, полка; углы — запил 45° или профиль; за коробом плитку не кладут.
8. Между коробом и углом полоса 16 мм — довести короб до угла.

Допущения и предложения на листе. Основа листа: размеры сняты со скана обмерного плана KV оформление (см): часть подписей не читается, помещения выровнены по читаемым размерам; контрольный обмер не выполнен (К-1); высота потолка 2650 мм принята по отметкам обмера (H = 2,50…2,66 м, ригель 2,28 м) — уточнить при обмере (К-2); толщины стен 300 / 120 мм приняты, межквартирная стена и колонны — по скану, не замерены (К-1); разрешённая мощность 15 кВт принята по типовым ТУ; при объединении двух квартир — переоформление ТУ (К-4); подрайон климата не задан — принят не северный (жилые от 2,5 м) (К-8). Знак «**» — предложено, не утверждено (согласовать): пол пом. 6, Св15, КУП1; ИЗ-1: Р8, ЭВ4, ЭВ6. См. лист открытых вопросов (лист 6, записи ИЗ-1, К-1, К-2, К-4, К-8).

| Изм. | Кол.уч | Лист | № док. | Подп. | Дата |
|---|---|---|---|---|---|
| Разраб. | | Кырлан А.С. | | | 04.11.26 |
| Пров. | | | | | |
| ГИП | | | | | |
| | | | | | |
| Н. контр. | | | | | |
| Утв. | | | | | |

**ГД-2026-009-АИ**

Квартира 103 м²

Общая площадь 100,72* м² · * размеры со скана, не замерены (реестр — л. 6, 7, К-1)

Дизайн-проект интерьера

| Стадия | Лист | Листов |
|---|---|---|
| РП | 51 | 120 |

**Раскладка плитки. Ванная. Развёртки стен**

М 1:25


**Кырлан Александр Сергеевич**

выпуск 04.11.2026 · 35b47f1c2a · стр. 57 из 130

# Раскладка плитки. Ванная мастер. Развёртки стен

ПРЕДВАРИТЕЛЬНО · не для производства работ · открыто пунктов: 8 (реестр — л. 6, 7)

Пом. 11 · вид изнутри помещения · размеры в мм · высоты от чистого пола, отметки от ±0,000

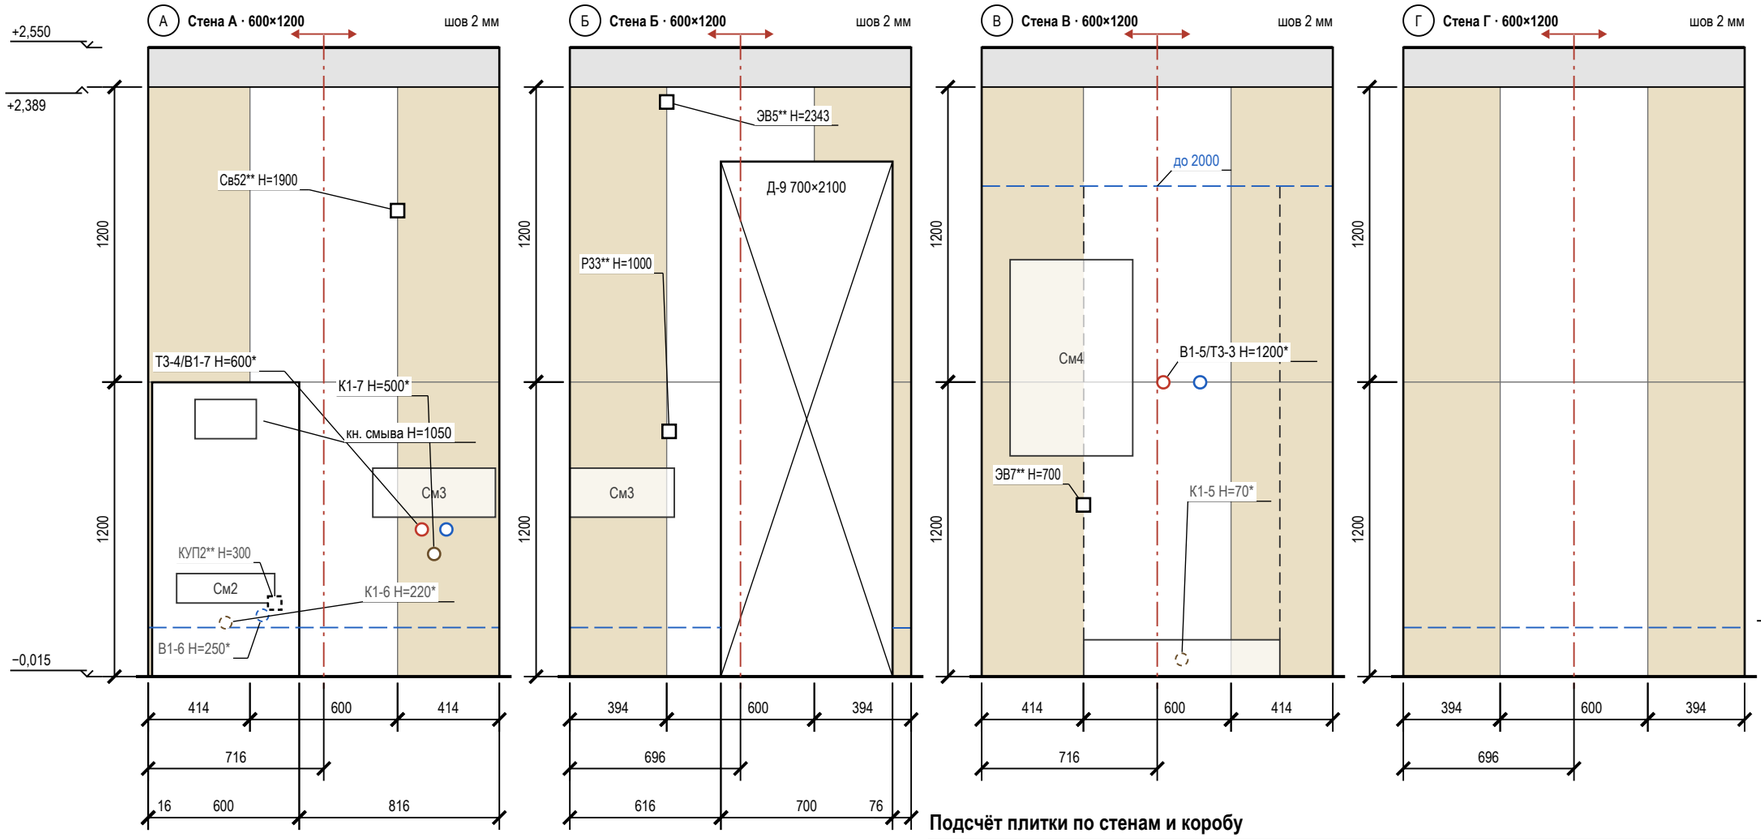


## Условные обозначения

- плитка целая; тонкая линия — шов
- плитка с подрезкой (размер — на цепочке)
- ось старта; стрелки — направление укладки
- верх гидроизоляции: 200 от ЧП, в мокрой зоне — «до …»
- проём — не облицовывается
- сантехприбор: габарит, высота по практике
- граница душевой зоны (ограждение)
- короб инсталляции, в нём кнопка смыва 250×160
- вывод В1 (код — в ведомости привязок)
- вывод Т3 (код — в ведомости привязок)
- вывод К1 (код — в ведомости привязок)
- вывод за прибором / в коробе (не на сетке)
- электроточка: марка и Н — по листам ЭОМ
- отметка уровня, м: ±0,000 — чистый пол жилых помещений
- низ потолка; серая полоса — стена без плитки
- (А) обозначение стены А–Г (как на развёртках)

## Подсчёт плитки по стенам и коробу

| Поверхность | L × H, мм | S, м² | Целых | Подр. | С запасом | Подрезки: край / верх, мм |
|---|---|---|---|---|---|---|
| стена А | 1432 × 2404 | 2,84 | 1 | 5 | 7 | 414 / 414; целый ряд |
| короб (ст. А) | 600×1200×250 | 1,47 | 1 | 3 | 5 | лицо 600; бок. 250 |
| стена Б | 1392 × 2404 | 1,99 | 0 | 6 | 7 | 394 / 394; целый ряд |
| стена В | 1432 × 2404 | 3,56 | 2 | 4 | 7 | 414 / 414; целый ряд |
| стена Г | 1392 × 2404 | 3,46 | 2 | 4 | 7 | 394 / 394; целый ряд |
| **Итого** | | **13,32** | **6** | **22** | **33** | |

## Примечания

1. Вид изнутри, стены по часовой стрелке А → Г. Высоты — от чистого пола (−0,015), отметки — от ±0,000. Раскладка от чистовых размеров (штукатурка 10 + клей 5 + плитка 9 мм), подрезки чистые; старт — от оси стены, ряды от пола целыми.
2. Верх плитки +2,389, потолок +2,550, зазор 161 мм: потолок ГКЛ опустить до +2,392 (шов 3 мм, герметик) — согласовать с монтажником ГКЛ; иначе профиль-окантовка, полосу окрасить в цвет потолка. Подрезной ряд 156 мм не делать.
3. Открытые выводы и электроточки — на шве или в центре плитки (допуск 10 мм; плитка от 900 мм по высоте — на шве или не ближе 60 мм к нему).
4. Выводы ВК стоят по оси прибора и с прибором не двигаются — привязки по «Плану выводов сантехники» без сдвига; вне сетки (Т3-4/В1-7, К1-7, В1-5/Т3-3) отверстие в плитке коронкой по той же привязке, плитку не сдвигать.
5. Выводы — по «Плану выводов сантехники», электроточки — по ЭОМ, «*» — высота по практике; за приборами и в коробе (В1-6, К1-6, КУП2**, К1-5) — штриховым кольцом.
6. Гидроизоляция: 200 мм от ЧП по периметру; у душа — до 2000 и 500 мм за поддон (СП 29.13330.2011, п. 7.2 — на высоту замачивания); углы — лентой; акт скрытых работ, пролив.
7. Короб 600×1200×250: лицо 600 мм от оси кнопки смыва, боковины, полка; углы — запил 45° или профиль; за коробом плитку не кладут.
8. Между коробом и углом полоса 16 мм — довести короб до угла.
9. Линии узора (швы плитки, складки штор, рёбра радиаторов) прерываются у знаков и выносок — просвет между линиями не менее 0,7 мм.

Допущения и предложения на листе. Основа листа: размеры сняты со скана обмерного плана KV оформление (см): часть подписей не читается, помещения выровнены по читаемым размерам; контрольный обмер не выполнен (К-1); высота потолка 2650 мм принята по отметкам обмера (Н = 2,50…2,66 м, ригель 2,28 м) — уточнить при обмере (К-2); толщины стен 300 / 120 мм приняты, межквартирная стена и колонны — по скану, не замерены (К-1); разрешённая мощность 15 кВт принята по типовым ТУ; при объединении двух квартир — переоформление ТУ (К-4); подрайон климата не задан — принят не северный (жилые от 2,5 м) (К-8). Знак «**» — предложено, не утверждено (согласовать): пол пом. 11, Св52, ЭВ5, КУП2; ИЗ-1: Р33, ЭВ7. См. лист открытых вопросов (лист 6, записи ИЗ-1, К-1, К-2, К-4, К-8).

1000 мм · печать 1:1

| Изм. | Кол.уч | Лист | № док. | Подп. | Дата |
|---|---|---|---|---|---|
| Разраб. | | Кырлан А.С. | | | 04.11.26 |
| Пров. | | | | | |
| ГИП | | | | | |
| | | | | | |
| Н. контр. | | | | | |
| Утв. | | | | | |

**ГД-2026-009-АИ**

Квартира 103 м²

Общая площадь 100,72* м² · * размеры со скана, не замерены (реестр — л. 6, 7, К-1)

Дизайн-проект интерьера

| Стадия | Лист | Листов |
|---|---|---|
| РП | 52 | 120 |

**Раскладка плитки. Ванная мастер. Развёртки стен**

М 1:25

**Кырлан Александр Сергеевич**

выпуск 04.11.2026 № 35b47f1c2a · стр. 58 из 130

07

# Полы и отделка

Кырлан Александр Сергеевич

выпуск 04.11.2026 · 35b47f1c2a · стр. 59 из 130


# План полов

Покрытия, направление укладки, отметки чистого пола, стыки · размеры в мм · отметки в м

**ПРЕДВАРИТЕЛЬНО · не для производства работ · открыто пунктов: 8 (реестр — л. 6, 7)**

## Условные обозначения

- тип 1 — инженерная доска, линии — вдоль доски
- тип 2 — инженерная доска, линии — вдоль доски
- тип 3 — керамогранит 600×1200, сетка — формат плитки
- тип 4 — инженерная доска, линии — вдоль доски
- тип 5 — керамогранит 600×600, сетка — формат плитки
- 1 — номер типа пола (экспликация полов)
- схема пола, без масштаба: плита — штриховка, стяжка — точки, звукоизоляция — зигзаг, гидроизоляция — утолщённая линия с заведением на стену
- направление укладки (длинная сторона доски)
- отметка чистого пола, м
- стык в проёме: без порога (б/п)
- стык в проёме: решение не задано
- стык в проёме: порог
- CT1 — марка стыка (ведомость стыков)
- стояк: К1 — канализация, В1 ХВС, Т3 — ГВС
- 1 — номер помещения, площадь м²

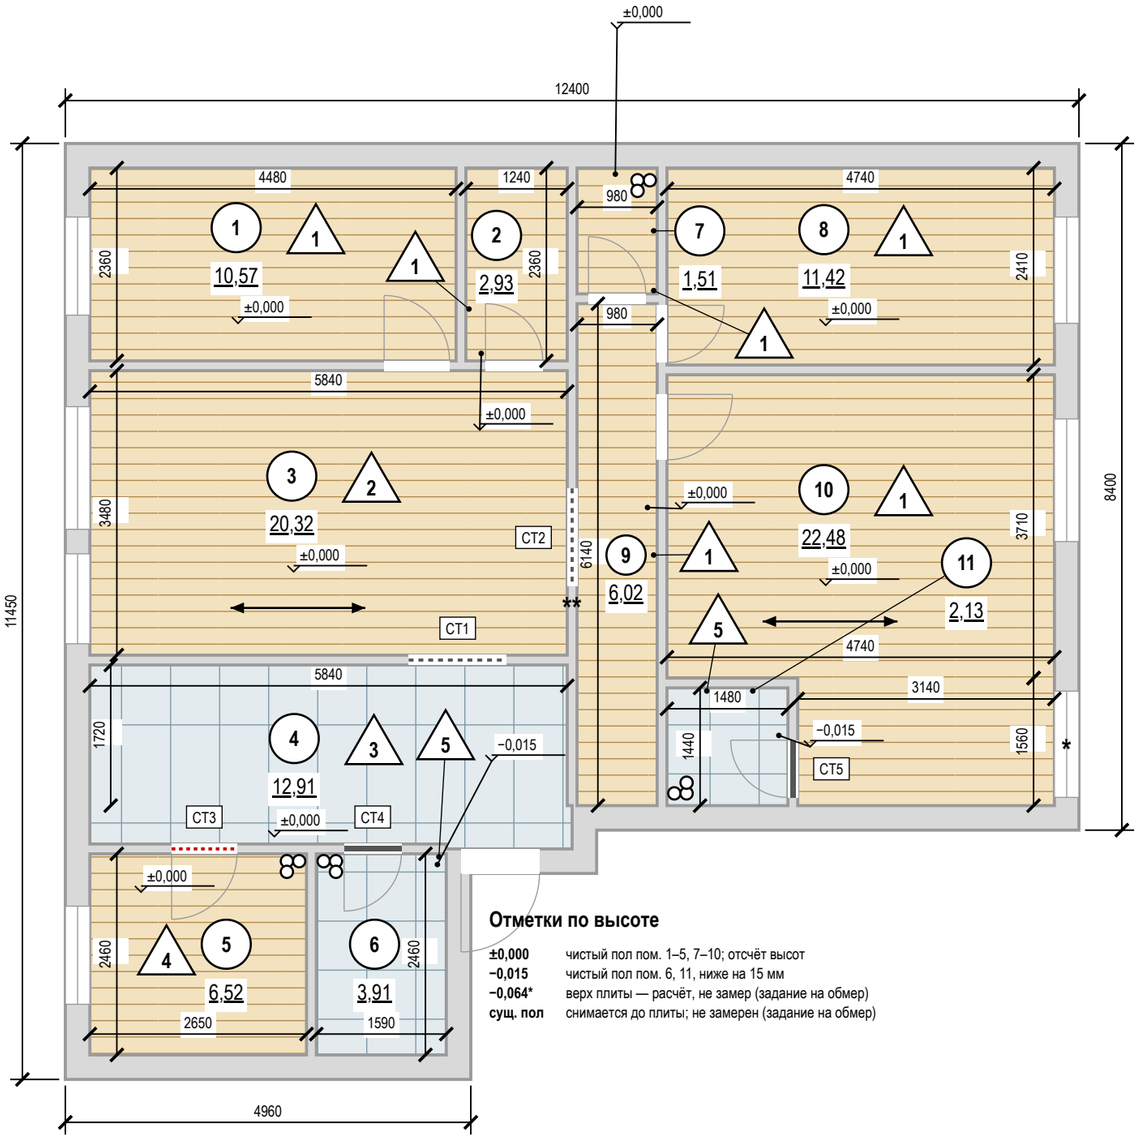


### Отметки по высоте

| | |
|---|---|
| **±0,000** | чистый пол пом. 1–5, 7–10; отсчёт высот |
| **−0,015** | чистый пол пом. 6, 11, ниже на 15 мм |
| **−0,064*** | верх плиты — расчёт, не замер (задание на обмер) |
| **сущ. пол** | снимается до плиты; не замерен (задание на обмер) |

## Экспликация полов

| Номер помещения | Тип пола | Схема пола | Данные элементов пола (наименование, толщина, основание), мм | Площадь, м² |
|---|---|---|---|---|
| 1, 2, 7, 8, 9, 10 | 1 | | Инженерная доска на клею — 14<br>Стяжка ЦПС М200 — 50<br>Плита перекрытия<br>Всего 64 мм; ЧП ±0,000, верх плиты −0,064 | 54,93 |
| 3 | 2 | | Инженерная доска дуб на клею — 14<br>Клей паркетный МС-полимерный — 1<br>Стяжка ЦПС М300 (В22,5), фибра, по звукоизоляции — 49<br>Плита перекрытия монолитная<br>Всего 64 мм; ЧП ±0,000, верх плиты −0,064 | 20,32 |
| 4 | 3 | | Керамогранит на клею С2 TE S1 — 14<br>Стяжка ЦПС М200 — 50<br>Плита перекрытия<br>Всего 64 мм; ЧП ±0,000, верх плиты −0,064 | 12,91 |
| 5 | 4 | | Инженерная доска дуб на клею — 14<br>Клей паркетный МС-полимерный — 1<br>Гидроизоляция полиуретановая, 2 слоя (зона мойки и острова) — 2<br>Стяжка ЦПС М300 (В22,5), фибра, по звукоизоляции — 47<br>Плита перекрытия монолитная<br>Всего 64 мм; ЧП ±0,000, верх плиты −0,064 | 6,52 |
| 6, 11 | 5 | | Керамогранит на клею С2 TE S1 — 14<br>Гидроизоляция обмазочная, 2 слоя, с заведением на стены 200 мм — 2<br>Стяжка ЦПС М200 — 33<br>Плита перекрытия<br>Всего 49 мм; ЧП −0,015, верх плиты −0,064 | 6,04 |
| | | | **Итого** | **100,72** |

## Стыки покрытий в проёмах

| Марка | Проём | Типы пола | Отметки ЧП | Решение |
|---|---|---|---|---|
| CT1 | 3–4 | 2 / 3 | ±0,000 / ±0,000 | б/п |
| CT2 | 3–9 | 2 / 1 | ±0,000 / ±0,000 | б/п |
| CT3 | 5–4 (Д-4) | 4 / 3 | ±0,000 / ±0,000 | не задано |
| CT4 | 6–4 (Д-5) | 5 / 3 | −0,015 / ±0,000 | порог h=15 мм |
| CT5 | 11–10 (Д-9) | 5 / 1 | −0,015 / ±0,000 | порог h=15 мм |

Допущения и предложения на листе. Знак «*» принято (замерить): Ст К1-3, Ст В1-3, Ст Т3-3. Знак «**» предложено (согласовать): плинтус пом. 1–5, 7–10, акцент пом. 3, фартук пом. 5, пол пом. 6, 11. См. лист открытых вопросов (лист 6).

## Примечания

1. За отметку ±0,000 принят чистый пол, не существующий (блок отметок). Площади — по чистым размерам помещений, м²; размеры — в мм.
2. Стык разнотипных покрытий — по оси дверного полотна (под полотном в закрытом положении); решение стыка — по ведомости стыков.
3. Размеры помещений в свету (ширина × длина, мм), не поместившиеся на плане: пом. 4 — 5840 × 1720, 5900 × 470, 1540 × 60; пом. 7 — 980 × 1540.
4. Пол санузлов ниже смежных помещений на 15 мм за счёт меньшей толщины стяжки (верх плиты общий — по экспликации полов); гидроизоляция по стяжке с заведением на стены не менее 200 мм (СП 29.13330.2011, п. 7.2), до облицовки — тест проливом и акт скрытых работ.
5. Трубопроводы в конструкции пола не прокладываются: пирог пола 49–64 мм не вмещает выпуски канализации с уклоном — выпуски К1 ведутся по стенам над чистым полом в коробах (лист 34).
6. Звукоизоляционный слой под стяжкой проектом не предусмотрен (стяжка по плите): приведённый уровень ударного шума перекрытия с полом Lnw не более 60 дБ (СП 51.13330.2011, табл. 2) подтвердить по данным дома; при превышении — плавающая стяжка по звукоизоляции с демпферной лентой по контуру и у стояков, пирог пересчитать.
7. Штучные покрытия (инженерная доска): направление — по стрелке; влажность основания по СМ не более 2,0 % (по ТУ изготовителя).
8. Ровность основания — просвет под 2-метровой рейкой не более 2 мм: пом. 1, 2, 3, 5, 7, 8, 9, 10 (инженерная доска), пом. 4, 6, 11 (керамогранит); проверить до укладки покрытия (СП 71.13330.2017, табл. 8.5).
9. Сетка на плитке — условная, в размер формата; точка старта и раскладка — по листу раскладки плитки.
10. Узор покрытия (заливка-код типа пола) прерывается под надписями — площадями помещений и отметками чистого пола.
11. Пироги полов — по экспликации полов: слои сверху вниз, толщины в мм; гидроизоляция мокрых зон — в пироге и в ведомости отделки; схема пола — без масштаба.

1000 мм · печать 1:1

| Изм. | Кол.уч | Лист | № док. | Подп. | Дата |
|---|---|---|---|---|---|
| Разраб. | | Кырлан А.С. | | | 04.11.26 |
| Пров. | | | | | |
| ГИП | | | | | |
| | | | | | |
| Н. контр. | | | | | |
| Утв. | | | | | |

**ГД-2026-009-АИ**

Квартира 103 м²

Общая площадь 100,72* м² · * размеры со скана, не замерены (реестр — л. 6, 7, К-1)

Дизайн-проект интерьера

| Стадия | Лист | Листов |
|---|---|---|
| РП | 53 | 120 |

**План полов**

М 1:75

**Кырлан Александр Сергеевич**

выпуск 04.11.2026 № 35b47f1c2a · стр. 60 из 130

# Ведомость отделки помещений. Лист 1 из 3

ПРЕДВАРИТЕЛЬНО · не для производства работ · открыто пунктов: 8 (реестр — л. 6, 7)

Потолки, стены, низ стен, полы · площади в м², длины в м · отметки в м

### Ведомость отделки помещений (форма 1 прил. А ГОСТ 21.501-2018). Лист 1 из 3

| № | Наименование помещения | Потолок | | | Стены и перегородки | | | Низ стен (плинтус) | | | Пол | | Примечание |
|---|---|---|---|---|---|---|---|---|---|---|---|---|---|
| | | Вид отделки | Код цвета | S, м² | Вид отделки | Код цвета | S, м² | Вид отделки | Код цвета | L, м | Вид отделки | S, м² | |
| 1 | Кабинет-библиотека<br>10,57 м² | ГКЛ по каркасу П113, отм. +2,550;<br>окраска, Tikkurila Anti-Reflex 2,<br>глубокоматовая, 2 слоя, подготовка<br>Q3 | NCS S 0502-Y | 10,57 | Окраска, Farrow & Ball Modern Emulsion,<br>матовая, 2 слоя, подготовка Q3<br><br>Акцент — стена А: окраска, Farrow &<br>Ball Modern Emulsion, матовая, 2 слоя,<br>подготовка Q3 | Farrow & Ball<br>No. 291<br><br>Farrow & Ball<br>No. 289 | 19,91<br><br>11,42 | Плинтус МДФ h=83 мм,<br>Ultrawood Base 5340, ЛДФ<br>под окраску, 83×15 мм,<br>2440 мм (арт.<br>LDF-BASE-5340) | Farrow & Ball<br>No. 291 | 12,9 | Инженерная доска, 1167-4250,<br>2100×127 мм, на клею; тип 1, отм.<br>ЧП ±0,000 | 10,57 | Н стен 2550 (до потолка);<br>плинтус в цвет: стены |
| 2 | Кладовая<br>2,93 м² | Существующий потолок, отм. +2,650;<br>окраска, Tikkurila Anti-Reflex 2,<br>глубокоматовая, 2 слоя, подготовка<br>Q3 | NCS S 0502-Y | 2,93 | Окраска, Tikkurila Harmony, матовая, 2<br>слоя, подготовка Q3 | NCS S 0502-Y | 17,61 | Плинтус МДФ h=83 мм,<br>Ultrawood Base 5340, ЛДФ<br>под окраску, 83×15 мм,<br>2440 мм (арт.<br>LDF-BASE-5340) | NCS S 0502-Y | 6,5 | Инженерная доска, 1167-4250,<br>2100×127 мм, на клею; тип 1, отм.<br>ЧП ±0,000 | 2,93 | Н стен 2650 (до потолка);<br>плинтус в цвет: стены |
| 3 | Гостиная-столовая<br>20,32 м² | ГКЛ по каркасу П113, отм. +2,550;<br>окраска, Farrow & Ball Modern<br>Emulsion, матовая, 2 слоя,<br>подготовка Q3 | Farrow & Ball<br>No. 291 | 20,32 | Окраска, Farrow & Ball Modern Emulsion,<br>матовая, 2 слоя, подготовка К3<br>Акцент — стена А: окраска, Farrow &<br>Ball Modern Emulsion, матовая, 3 слоя,<br>аналог: интерьерная краска Farrow &<br>Ball Modern Emulsion в цвете веера No.<br>255, матовая, подготовка К3 | Farrow & Ball<br>No. 291<br>Farrow & Ball<br>No. 255 | 23,57<br><br>11,74 | Плинтус МДФ h=83 мм,<br>Ultrawood Base 5340, ЛДФ<br>под окраску, 83×15 мм,<br>2440 мм (арт.<br>LDF-BASE-5340) | Farrow & Ball<br>No. 291 | 14,7 | Инженерная доска, 1167-4250,<br>2100×127 мм, на клею; тип 2, отм.<br>ЧП ±0,000 | 20,32 | Н стен 2550 (до потолка);<br>класс мокрого истирания по<br>EN 13300 и блеск линейки<br>Farrow & Ball Modern<br>Emulsion — по ТУ<br>производителя, в базе не<br>сверены; потолок в цвет<br>стен (No. 291) — краска<br>бренда веера, Farrow & Ball<br>Modern Emulsion;<br>класс мокрого истирания по<br>EN 13300 и блеск линейки<br>Farrow & Ball Modern<br>Emulsion — по ТУ<br>производителя, в базе не<br>сверены; колеруется в код<br>стен, но по эмали на МДФ:<br>сличать отдельным выкрасом<br>на своей подложке (выкрас №<br>10); плинтус в цвет: стены |
| 4 | Прихожая-холл<br>12,91 м² | ГКЛ по каркасу П113, отм. +2,550;<br>окраска, Tikkurila Anti-Reflex 2,<br>глубокоматовая, 2 слоя, подготовка<br>Q3 | NCS S 0502-Y | 12,91 | Окраска, Farrow & Ball Modern Emulsion,<br>матовая, 2 слоя, подготовка Q3 | Farrow & Ball<br>No. 291 | 33,88 | Плинтус МДФ h=83 мм,<br>Ultrawood Base 5340, ЛДФ<br>под окраску, 83×15 мм,<br>2440 мм (арт.<br>LDF-BASE-5340) | Farrow & Ball<br>No. 291 | 12,6 | Керамогранит, A8UZ, 600×1200×9 мм;<br>тип 3, отм. ЧП ±0,000 | 12,91 | Н стен 2550 (до потолка);<br>матовая моющаяся, класс 1<br>EN 13300 — осознанно вместо<br>полуматовой; плинтус в<br>цвет: стены |

### Примечания

1. Ведомость продолжена на листе 2 из 3; итоги, сводка площадей и примечания — на последнем листе ведомости.

**Допущения и предложения на листе**

Основа листа: размеры сняты со скана обмерного плана KV оформление (см): часть подписей не читается, помещения выровнены по читаемым размерам; контрольный обмер не выполнен (К-1); высота потолка 2650 мм принята по отметкам обмера (Н = 2,50…2,66 м, ригель 2,28 м) — уточнить при обмере (К-2); толщины стен 300 / 120 мм приняты, межквартирная стена и колонны — по скану, не замерены (К-1); разрешённая мощность 15 кВт принята по типовым ТУ; при объединении двух квартир — переоформление ТУ (К-4); подрайон климата не задан — принят не северный (жилые от 2,5 м) (К-8).

Знак «**» — предложение проектировщика, заказчиком не утверждено (согласовать с заказчиком): плинтус пом. 1–5, 7–10, акцент пом. 3, фартук пом. 5 — артикул изделия не выбран: позиция описана характеристиками («аналог по характеристикам»), артикул выбирается при закупке; пол пом. 6, 11 — пирог пола: стяжка 33 мм и обмазочная гидроизоляция добавлены разработчиком проекта; артикул изделия не выбран: позиция описана характеристиками («аналог по характеристикам»), артикул выбирается при закупке.

См. лист открытых вопросов (лист 6, записи К-1, К-2, К-4, К-8).

| Изм. | Кол.уч | Лист | № док. | Подп. | Дата |
|---|---|---|---|---|---|
| Разраб. | | Кырлан А.С. | | | 04.11.26 |
| Пров. | | | | | |
| ГИП | | | | | |
| | | | | | |
| Н. контр. | | | | | |
| Утв. | | | | | |

**ГД-2026-009-АИ**

Квартира 103 м²

Общая площадь 100,72* м² · * размеры со скана, не замерены (реестр — л. 6, 7, К-1)

| Дизайн-проект интерьера | Стадия | Лист | Листов |
|---|---|---|---|
| | РП | 54 | 120 |

**Ведомость отделки помещений. Лист 1 из 3**

М б/м

**Кырлан Александр Сергеевич**

выпуск 04.11.2026 № 35b47f1c2a · стр. 61 из 130

# Ведомость отделки помещений. Лист 2 из 3

Потолки, стены, низ стен, полы · площади в м², длины в м · отметки в м

## Ведомость отделки помещений (форма 1 прил. А ГОСТ 21.501-2018). Лист 2 из 3

| № | Наименование помещения | Потолок | | | Стены и перегородки | | | Низ стен (плинтус) | | | Пол | | Примечание |
|---|---|---|---|---|---|---|---|---|---|---|---|---|---|
| | | Вид отделки | Код цвета | S, м² | Вид отделки | Код цвета | S, м² | Вид отделки | Код цвета | L, м | Вид отделки | S, м² | |
| 5 | Кухня<br>6,52 м² | ГКЛВ по каркасу П113, отм. +2,550; окраска, Farrow & Ball Modern Emulsion, матовая, 2 слоя, подготовка Q3 | Farrow & Ball No. 291 | 6,52 | Окраска, Farrow & Ball Modern Emulsion, матовая, 2 слоя, подготовка К3<br>Фартук кухни (стена Б, В): облицовка керамогранитом, аналог: керамогранит матовый, тон F497, 600×600×9 мм, клей C2 TE S1, затирка CG2WA | Farrow & Ball No. 291<br>#F1F1EC | 20,51<br>2,01 | Плинтус МДФ h=83 мм, Ultrawood Base 5340, ЛДФ под окраску, 83×15 мм, 2440 мм (арт. LDF-BASE-5340) | Farrow & Ball No. 291 | 9,4 | Инженерная доска, 1167-4250, 2100×127 мм, на клею; тип 4, отм. ЧП ±0,000 | 6,52 | Н стен 2550 (до потолка); моющаяся матовая окраска Farrow & Ball Modern Emulsion (краска бренда веера No. 291,); класс мокрого истирания по EN 13300 и блеск линейки Farrow & Ball Modern Emulsion — по ТУ производителя, в базе не сверены; категория К3 по СП 71.13330.2017, табл. 7.5; по ГКЛ каркаса П113, моющаяся окраска Farrow & Ball Modern Emulsion; Q3 класс мокрого истирания по EN 13300 и блеск линейки Farrow & Ball Modern Emulsion — по ТУ производителя, в базе не сверены; колеруется в код стен, но по эмали на МДФ: сличать отдельным выкрасом на своей подложке (выкрас № 10); плинтус в цвет: стены |
| 6 | Ванная<br>3,91 м² | ГКЛВ по каркасу П113, отм. +2,550; окраска, Tikkurila Luja 7, матовая, 2 слоя, подготовка Q3 | NCS S 0502-Y | 3,91 | Облицовка плиткой, A8UZ, 600×1200×9 мм, клей C2 TE S1, затирка CG2WA | Atlas Concorde A8UZ | 18,00 | нет | | | Керамогранит, Atlas Concorde Marvel Travertine Sand CrossMatte Sensitech, арт. AFUL (той же коллекции, что стены A8UZ; тон сверить по образцу), 600×600×9 мм; тип 5, отм. ЧП −0,015 | 3,91 | Н стен 2565 (до потолка); гидроизоляция обмазочная, 2 слоя, с заведением на стены 200 мм; над ванной — до 2000 и 300 мм за борт (по пирогу пола); тест проливом и акт скрытых работ |
| 7 | Постирочная<br>1,51 м² | Существующий потолок, отм. +2,650; окраска, Tikkurila Anti-Reflex 2, глубокоматовая, 2 слоя, подготовка Q3 | NCS S 0502-Y | 1,51 | Окраска, Tikkurila Harmony, матовая, 2 слоя, подготовка Q3 | NCS S 0502-Y | 11,89 | Плинтус МДФ h=83 мм, Ultrawood Base 5340, ЛДФ под окраску, 83×15 мм, 2440 мм (арт. LDF-BASE-5340) | NCS S 0502-Y | 4,3 | Инженерная доска, 1167-4250, 2100×127 мм, на клею; тип 1, отм. ЧП ±0,000 | 1,51 | Н стен 2650 (до потолка); плинтус в цвет: стены |
| 8 | Спальня 2<br>11,42 м² | ГКЛ по каркасу П113, отм. +2,550; окраска, Tikkurila Anti-Reflex 2, глубокоматовая, 2 слоя, подготовка Q3 | NCS S 0502-Y | 11,42 | Окраска, Farrow & Ball Modern Emulsion, матовая, 2 слоя, подготовка Q3<br><br>Акцент — стена А: окраска, Farrow & Ball Modern Emulsion, матовая, 2 слоя, подготовка Q3 | Farrow & Ball No. 291<br><br>Farrow & Ball No. 289 | 20,89<br><br>12,09 | Плинтус МДФ h=83 мм, Ultrawood Base 5340, ЛДФ под окраску, 83×15 мм, 2440 мм (арт. LDF-BASE-5340) | Farrow & Ball No. 291 | 13,6 | Инженерная доска, 1167-4250, 2100×127 мм, на клею; тип 1, отм. ЧП ±0,000 | 11,42 | Н стен 2550 (до потолка); плинтус в цвет: стены |
| 9 | Коридор<br>6,02 м² | ГКЛ по каркасу П113, отм. +2,550; окраска, Tikkurila Anti-Reflex 2, глубокоматовая, 2 слоя, подготовка Q3 | NCS S 0502-Y | 6,02 | Окраска, Farrow & Ball Modern Emulsion, матовая, 2 слоя, подготовка Q3 | Farrow & Ball No. 291 | 29,17 | Плинтус МДФ h=83 мм, Ultrawood Base 5340, ЛДФ под окраску, 83×15 мм, 2440 мм (арт. LDF-BASE-5340) | Farrow & Ball No. 291 | 10,8 | Инженерная доска, 1167-4250, 2100×127 мм, на клею; тип 1, отм. ЧП ±0,000 | 6,02 | Н стен 2550 (до потолка); матовая моющаяся, класс 1 EN 13300 — осознанно вместо полуматовой; плинтус в цвет: стены |

### Примечания

1. Ведомость продолжена на листе 3 из 3; итоги, сводка площадей и примечания — на последнем листе ведомости.

**Допущения и предложения на листе**

Основа листа: размеры сняты со скана обмерного плана KV оформление (см): часть подписей не читается, помещения выровнены по читаемым размерам; контрольный обмер не выполнен (К-1); высота потолка 2650 мм принята по отметкам обмера (Н = 2,50…2,66 м, ригель 2,28 м) — уточнить при обмере (К-2); толщины стен 300 / 120 мм приняты, межквартирная стена и колонны — по скану, не замерены (К-1); разрешённая мощность 15 кВт принята по типовым ТУ; при объединении двух квартир — переоформление ТУ (К-4); подрайон климата не задан — принят не северный (жилые от 2,5 м) (К-8).

Знак «**» — предложение проектировщика, заказчиком не утверждено (согласовать с заказчиком): плинтус пом. 1–5, 7–10, акцент пом. 3, фартук пом. 5 — артикул изделия не выбран: позиция описана характеристиками («аналог по характеристикам»), артикул выбирается при закупке; пол пом. 6, 11 — пирог пола: стяжка 33 мм и обмазочная гидроизоляция добавлены разработчиком проекта; артикул изделия не выбран: позиция описана характеристиками («аналог по характеристикам»), артикул выбирается при закупке.

См. лист открытых вопросов (лист 6, записи К-1, К-2, К-4, К-8).

| Изм. | Кол.уч | Лист | № док. | Подп. | Дата |
|---|---|---|---|---|---|
| Разраб. | | Кырлан А.С. | | | 04.11.26 |
| Пров. | | | | | |
| ГИП | | | | | |
| | | | | | |
| Н. контр. | | | | | |
| Утв. | | | | | |

**ГД-2026-009-АИ**

Квартира 103 м²

Общая площадь 100,72* м² · * размеры со скана, не замерены (реестр — л. 6, 7, К-1)

| Дизайн-проект интерьера | Стадия | Лист | Листов |
|---|---|---|---|
| | РП | 55 | 120 |

**Ведомость отделки помещений. Лист 2 из 3**

М б/м

**Кырлан Александр Сергеевич**

выпуск 04.11.2026 № 35b47f1c2a · стр. 62 из 130

# Ведомость отделки помещений. Лист 3 из 3



Потолки, стены, низ стен, полы · площади в м², длины в м · отметки в м

### Ведомость отделки помещений (форма 1 прил. А ГОСТ 21.501-2018). Лист 3 из 3

| № | Наименование помещения | Потолок | | | Стены и перегородки | | | Низ стен (плинтус) | | | Пол | | Примечание |
|---|---|---|---|---|---|---|---|---|---|---|---|---|---|
| | | Вид отделки | Код цвета | S, м² | Вид отделки | Код цвета | S, м² | Вид отделки | Код цвета | L, м | Вид отделки | S, м² | |
| 10 | Спальня мастер<br>22,48 м² | ГКЛ по каркасу П113, отм. +2,550;<br>окраска, Tikkurila Anti-Reflex 2,<br>глубокоматовая, 2 слоя, подготовка<br>Q3 | NCS S 0502-Y | 22,48 | Окраска, Farrow & Ball Modern Emulsion,<br>матовая, 2 слоя, подготовка Q3<br><br>Акцент — стена А: окраска, Farrow &<br>Ball Modern Emulsion, матовая, 2 слоя,<br>подготовка Q3 | Farrow & Ball<br>No. 291<br><br>Farrow & Ball<br>No. 289 | 31,48<br><br>12,09 | Плинтус МДФ h=83 мм,<br>Ultrawood Base 5340, ЛДФ<br>под окраску, 83×15 мм,<br>2440 мм (арт.<br>LDF-BASE-5340) | Farrow & Ball<br>No. 291 | 18,5 | Инженерная доска, 1167-4250,<br>2100×127 мм, на клею; тип 1, отм.<br>ЧП ±0,000 | 22,48 | Н стен 2550 (до потолка);<br>плинтус в цвет: стены |
| 11 | Ванная мастер<br>2,13 м² | ГКЛВ по каркасу П113, отм. +2,550;<br>окраска, Tikkurila Luja 7, матовая,<br>2 слоя, подготовка Q3 | NCS S 0502-Y | 2,13 | Облицовка плиткой, A8UZ, 600×1200×9 мм,<br>клей C2 TE S1, затирка CG2WA | Atlas Concorde<br>A8UZ | 12,57 | нет | | | Керамогранит, Atlas Concorde Marvel<br>Travertine Sand CrossMatte<br>Sensitech, арт. AFUL (той же<br>коллекции, что стены A8UZ; тон<br>сверить по образцу), 600×600×9 мм;<br>тип 5, отм. ЧП −0,015 | 2,13 | Н стен 2565 (до потолка);<br>гидроизоляция обмазочная, 2<br>слоя, с заведением на стены<br>200 мм; у душа — до 2000 и<br>500 мм за поддон (по пирогу<br>пола); тест проливом и акт<br>скрытых работ |
| | **Итого** | | | **100,72** | | | **288,83** | | | **103,5** | | **100,72** | |

### Сводка площадей по материалам отделки

| Поверхность | Материал / код цвета | Серия | Площадь, м² |
|---|---|---|---|
| Потолок | NCS S 0502-Y | Anti-Reflex 2 | 67,84 |
| Потолок | Farrow & Ball No. 291 | Modern Emulsion | 26,84 |
| Потолок | NCS S 0502-Y | Luja 7 | 6,04 |
| Стены | Farrow & Ball No. 291 | Modern Emulsion | 179,41 |
| Стены | Farrow & Ball No. 289 | Modern Emulsion | 35,60 |
| Стены | NCS S 0502-Y | Harmony | 29,50 |
| Стены | Farrow & Ball No. 255 | Modern Emulsion | 11,74 |
| Стены | облицовка плиткой 600×1200×9 мм,<br>Atlas Concorde A8UZ | A8UZ | 30,57 |
| Фартук | облицовка керамогранитом, #F1F1EC | аналог: керамогранит<br>матовый, тон F497 | 2,01 |

**Допущения и предложения на листе**

Основа листа: размеры сняты со скана обмерного плана KV оформление (см): часть подписей не читается, помещения выровнены по читаемым размерам; контрольный обмер не выполнен (К-1); высота потолка 2650 мм принята по отметкам обмера (Н = 2,50…2,66 м, ригель 2,28 м) — уточнить при обмере (К-2); толщины стен 300 / 120 мм приняты, межквартирная стена и колонны — по скану, не замерены (К-1); разрешённая мощность 15 кВт принята по типовым ТУ; при объединении двух квартир — переоформление ТУ (К-4); подрайон климата не задан — принят не северный (жилые от 2,5 м) (К-8).

Знак «**» — предложение проектировщика, заказчиком не утверждено (согласовать с заказчиком): плинтус пом. 1–5, 7–10, акцент пом. 3, фартук пом. 5 — артикул изделия не выбран: позиция описана характеристиками («аналог по характеристикам»), артикул выбирается при закупке; пол пом. 6, 11 — пирог пола: стяжка 33 мм и обмазочная гидроизоляция добавлены разработчиком проекта; артикул изделия не выбран: позиция описана характеристиками («аналог по характеристикам»), артикул выбирается при закупке.

См. лист открытых вопросов (лист 6, записи К-1, К-2, К-4, К-8).

## Примечания

1. Площади поверхностей — по чистым граням стен до отделки: стены = периметр × высоту от чистого пола помещения до низа потолка минус проёмы (облицовка плиткой — до верха облицовки); плинтус = периметр минус дверные проёмы; пол и потолок — по площади помещения. Количество плиток по раскладке. Площади помещений — с учётом всех частей помещения; откосы в площадь стен не входят.
2. Акцентные стены и фартук — отдельными строками, их площадь вычтена из основной отделки стен помещения; фартук — над нижними модулями кухни от столешницы до низа навесных шкафов, где шкафов нет — на 600 мм.
3. Плинтус — длина по периметру за вычетом дверных проёмов; примыкания к наличникам и встроенной мебели — по развёрткам.
4. Формат плитки — Ш×В×Т (ширина × высота в положении укладки × толщина), мм; на полу — вдоль стен А/В × вдоль стен Б/Г.
5. Коды цвета — по веерам производителей; колеровка каждой краски одной партией, проверка выкраса при свете D65 и при лампах проекта.
6. Уровни подготовки Q1–Q4 — система Knauf, не норма ГОСТ/СП; допуски поверхностей — по СП 71.13330.2017 (действующая редакция).
7. «аналог:» — изделие задано характеристиками, марку и артикул согласовать с заказчиком до закупки.
8. Плавающая стяжка по звукоизоляции: демпферная (кромочная) лента по контуру помещения и у стояков (СП 51.13330.2011, п. 9.11); плинтус крепится только к стене.

| | | | | | | |
|---|---|---|---|---|---|---|
| | | | | | | **ГД-2026-009-АИ** |
| | | | | | | Квартира 103 м²<br>Общая площадь 100,72* м² · * размеры со скана, не замерены (реестр — л. 6, 7, К-1) |
| Изм. | Кол.уч | Лист | № док. | Подп. | Дата | |
| Разраб. | | Кырлан А.С. | | | 04.11.26 | Дизайн-проект интерьера |
| Пров. | | | | | | Стадия: РП · Лист: 56 · Листов: 120 |
| ГИП | | | | | | |
| Н. контр. | | | | | | **Ведомость отделки помещений. Лист 3 из 3**<br>М б/м |
| Утв. | | | | | | **Кырлан Александр Сергеевич** |

# Колерная карта

Цвета и материалы по помещениям · палитра проекта · лист 1 из 2

## Колерная карта по помещениям

| Помещение | Поверхность | Образец | Поз. | Система и код цвета | Производитель, линейка / материал, артикул | Блеск | Класс истирания | LRV | Площадь |
|---|---|---|---|---|---|---|---|---|---|
| **1. Кабинет-библиотека** 10,57 м² | стены | | **K1** | Farrow & Ball No. 291 | Farrow & Ball · Modern Emulsion | матовая | 1 | 73 | 19,9 м² |
| | акцент А | | **K2** | Farrow & Ball No. 289 | Farrow & Ball · Modern Emulsion | матовая | 1 | 13 | 11,4 м² |
| | потолок | | **K3** | NCS S 0502-Y | Tikkurila · Anti-Reflex 2 | глубокомат. | 2 | 95 | 10,6 м² |
| | пол | | **KM1** | по образцу | Coswick · Вековые традиции · арт. 1167-4250 | | | | 10,6 м² |
| | плинтус | | **K4** | Farrow & Ball No. 291 | МДФ · в цвет Farrow & Ball | | | 73 | 12,9 м |
| **2. Кладовая** 2,93 м² | стены | | **K5** | NCS S 0502-Y | Tikkurila · Harmony | матовая | 1 | 95 | 17,6 м² |
| | потолок | | **K3** | NCS S 0502-Y | Tikkurila · Anti-Reflex 2 | глубокомат. | 2 | 95 | 2,9 м² |
| | пол | | **KM1** | по образцу | Coswick · Вековые традиции · арт. 1167-4250 | | | | 2,9 м² |
| | плинтус | | **K6** | NCS S 0502-Y | МДФ · в цвет NCS | | | 95 | 6,5 м |
| **3. Гостиная-столовая** 20,32 м² | стены | | **K1** | Farrow & Ball No. 291 | Farrow & Ball · Modern Emulsion | матовая | 1 | 73 | 23,6 м² |
| | акцент А | | **K7** | Farrow & Ball No. 255 | Farrow & Ball · Modern Emulsion | матовая | 1 | 7 | 11,7 м² |
| | потолок | | **K1** | Farrow & Ball No. 291 | Farrow & Ball · Modern Emulsion | матовая | 1 | 73 | 20,3 м² |
| | пол | | **KM1** | по образцу | Coswick · Вековые традиции · арт. 1167-4250 | | | | 20,3 м² |
| | плинтус | | **K8** | Farrow & Ball No. 291 | МДФ · в цвет Farrow & Ball | полуглянц. | 2 | 73 | 14,7 м |
| **4. Прихожая-холл** 12,91 м² | стены | | **K1** | Farrow & Ball No. 291 | Farrow & Ball · Modern Emulsion | матовая | 1 | 73 | 33,9 м² |
| | потолок | | **K3** | NCS S 0502-Y | Tikkurila · Anti-Reflex 2 | глубокомат. | 2 | 95 | 12,9 м² |
| | пол | | **KM2** | Marvel Travertine | Atlas Concorde · арт. A8UZ | | | | 12,9 м² |
| | плинтус | | **K4** | Farrow & Ball No. 291 | МДФ · в цвет Farrow & Ball | | | 73 | 12,6 м |
| **5. Кухня** 6,52 м² | стены | | **K1** | Farrow & Ball No. 291 | Farrow & Ball · Modern Emulsion | матовая | 1 | 73 | 20,5 м² |
| | потолок | | **K1** | Farrow & Ball No. 291 | Farrow & Ball · Modern Emulsion | матовая | 1 | 73 | 6,5 м² |
| | пол | | **KM1** | по образцу | Coswick · Вековые традиции · арт. 1167-4250 | | | | 6,5 м² |
| | плинтус | | **K8** | Farrow & Ball No. 291 | МДФ · в цвет Farrow & Ball | полуглянц. | 2 | 73 | 9,4 м |
| | фартук | | **KM3** | тон Paper F497 (тёплый белый) | керамогранит · аналог по хар. | | | | 2,0 м² |

**Допущения и предложения на листе**

Основа листа: размеры сняты со скана обмерного плана KV оформление (см): часть подписей не читается, помещения выровнены по читаемым размерам; контрольный обмер не выполнен (К-1); высота потолка 2650 мм принята по отметкам обмера (Н = 2,50…2,66 м, ригель 2,28 м) — уточнить при обмере (К-2); толщины стен 300 / 120 мм приняты, межквартирная стена и колонны — по скану, не замерены (К-1); разрешённая мощность 15 кВт принята по типовым ТУ; при объединении двух квартир — переоформление ТУ (К-4); подрайон климата не задан — принят не северный (жилые от 2,5 м) (К-8).


Знак «**» — предложение проектировщика, заказчиком не утверждено (согласовать с заказчиком): плинтус пом. 1–5, 7–10, акцент пом. 3, фартук пом. 5 — артикул изделия не выбран: позиция описана характеристиками («аналог по характеристикам»), артикул выбирается при закупке; пол пом. 6, 11 — пирог пола: стяжка 33 мм и обмазочная гидроизоляция добавлены разработчиком проекта; артикул изделия не выбран: позиция описана характеристиками («аналог по характеристикам»), артикул выбирается при закупке.

См. лист открытых вопросов (лист 6, записи К-1, К-2, К-4, К-8).

## Примечания

1. Цвет на листе и на экране — ориентир. До покраски — выкрас на объекте: не меньше А3 (или лист ГКЛ), на грунте под эту краску, не на белой шпаклёвке, в 2 слоя; на обороте — код, бренд, веер, дата. Смотреть днём и вечером, рядом с образцами пола и плитки. Красить только в цвет утверждённого выкраса.
2. Краску заказывать по коду из графы «Система и код цвета» у бренда этого кода, не «аналогом» другого; весь объём одного кода — одной партией, колеруемую краску — за один проход машины.
3. Площади — те же, что в ведомости отделки (лист 54); сколько краски заказать — в спецификации отделочных материалов (лист 59).
4. Колерная карта на 2 листах: обозначения — на каждом, схема и палитра — на первом, выкрасы — на последнем.

## Схема квартиры: цвет стен и акценты (б/м)

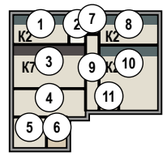



## Схема палитры проекта


Стиль: Мид-сенчури 65% + Ар-деко 35% · схема: комплементарная

| основной | основной | второстепенный | второстепенный | второстепенный | акцентный | акцентный | акцентный | акцентный |
|---|---|---|---|---|---|---|---|---|
| Farrow & Ball No. 291 | NCS S 0502-Y | Farrow & Ball No. 298 | Farrow & Ball No. 289 | Farrow & Ball No. 255 | NCS S 2050-Y20R | NCS S 3050-Y70R | NCS S 5030-B10G | NCS S 5040-B90G |
| School House White — тёплый меловой белый LRV 73 стены 1,3,4,5,8,9,10; плинтус 1,3,4,5,8,9,10; потолок 3,5; текстиль/декор 3 | Белый с лёгкой желтизной LRV 95 потолок 1,2,4,6,7,8,9,10,11; стены 2,7; плинтус 2,7; текстиль/декор 1,8,10 | Bancha — оливковый середины века LRV 14 текстиль/декор 3,10 | Inchyra Blue — тёмный сине-серый LRV 13 акцент 1,8,10; текстиль/декор 1,8,10 | Tanner's Brown — тёмный шоколад LRV 7 акцент 3; текстиль/декор 3 | Горчичный LRV 42 текстиль/декор 1,8 | Терракотовый / жжёный оранжевый LRV 18 текстиль/декор 1,8 | Тил LRV 12 текстиль/декор 8 | Изумрудный LRV 8 в отделке не применён |

План 60/30/10

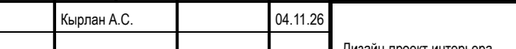


Окраска, факт — по площади стен, акцентов, потолков

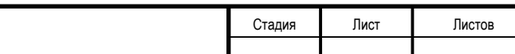


окрашено всего 357 м²; второстепенный тон несут мебель и текстиль

**Текстиль и декор в цветах вне палитры проекта**

NCS S 1005-Y20R Светлый кремовый — пом. 1 (T7), 3 (T1, T4), 5 (T14), 8 (T11), 10 (T19, T22)

## Условные обозначения

- **K1** Farrow & Ball No. 291 · School House White — тёплый меловой белый · Modern Emulsion · матовая · кл. 1
- **K2** Farrow & Ball No. 289 · Inchyra Blue — тёмный сине-серый · Modern Emulsion · матовая · кл. 1
- **K3** NCS S 0502-Y · Белый с лёгкой желтизной · Tikkurila Anti-Reflex 2 · глубокомат. · кл. 2
- **K4** Farrow & Ball No. 291 · School House White — тёплый меловой белый · МДФ
- **K5** NCS S 0502-Y · Белый с лёгкой желтизной · Tikkurila Harmony · матовая · кл. 1
- **K6** NCS S 0502-Y · Белый с лёгкой желтизной · МДФ
- **K7** Farrow & Ball No. 255 · Tanner's Brown — тёмный шоколад · Modern Emulsion · матовая · кл. 1
- дерево (доска, паркет, ламинат) — рисунок досок
- керамогранит, плитка, камень — сетка швов по формату
- **K8** Farrow & Ball No. 291 · School House White — тёплый меловой белый · МДФ · полуглянц. · кл. 2
- **K9** NCS S 0502-Y · Белый с лёгкой желтизной · Tikkurila Luja 7 · матовая · кл. 1
- **KM1** инженерная доска · 1167-4250
- **KM2** керамогранит · A8UZ
- **KM3** аналог: керамогранит матовый, тон F497, 600×600×9 мм
- **KM4** плитка · A8UZ
- **KM5** керамогранит · Atlas Concorde Marvel Travertine Sand Cross 60×60 Matte Sensitech, арт. AFUL (той же коллекции, что стены A8UZ; тон сверить по образцу)

К — краска, КМ — отделочный материал (тон КМ — по описанию, эталон — образец материала); кл. — класс истирания (1 — самый стойкий к мытью); LRV — светлота цвета: 0 — чёрный, 100 — белый

| Изм. | Кол.уч | Лист | № док. | Подп. | Дата |
|---|---|---|---|---|---|
| Разраб. | | Кырлан А.С. | | | 04.11.26 |
| Пров. | | | | | |
| ГИП | | | | | |
| Н. контр. | | | | | |
| Утв. | | | | | |

**ГД-2026-009-АИ**

Квартира 103 м²

Общая площадь 100,72* м² · * размеры со скана, не замерены (реестр — л. 6, 7, К-1)

Дизайн-проект интерьера

| Стадия | Лист | Листов |
|---|---|---|
| РП | 57 | 120 |

**Колерная карта**

М б/м

**Кырлан Александр Сергеевич**

выпуск 04.11.2026 № 35b47f1c2a · стр. 64 из 130

# Колерная карта

Цвета и материалы по помещениям · выкрасы на согласование · лист 2 из 2

## Колерная карта по помещениям (продолжение)

| Помещение | Поверхность | Образец | Поз. | Система и код цвета | Производитель, линейка / материал, артикул | Блеск | Класс истирания | LRV | Площадь |
|---|---|---|---|---|---|---|---|---|---|
| **6. Ванная** 3,91 м² | стены | | **КМ4** | Marvel Travertine | Atlas Concorde · арт. A8UZ | | | | 18,0 м² |
| | потолок | | **К9** | NCS S 0502-Y | Tikkurila · Luja 7 | матовая | 1 | 95 | 3,9 м² |
| | пол | | **КМ5** | по образцу | керамогранит · Atlas Concorde Marvel Travertine Sand Cross 60×60 Matte Sensitech, арт. AFUL (той же коллекции, что стены A8UZ; тон сверить по образцу) | | | | 3,9 м² |
| **7. Постирочная** 1,51 м² | стены | | **К5** | NCS S 0502-Y | Tikkurila · Harmony | матовая | 1 | 95 | 11,9 м² |
| | потолок | | **К3** | NCS S 0502-Y | Tikkurila · Anti-Reflex 2 | глубокомат. | 2 | 95 | 1,5 м² |
| | пол | | **КМ1** | по образцу | Coswick · Вековые традиции · арт. 1167-4250 | | | | 1,5 м² |
| | плинтус | | **К6** | NCS S 0502-Y | МДФ · в цвет NCS | | | 95 | 4,3 м |
| **8. Спальня 2** 11,42 м² | стены | | **К1** | Farrow & Ball No. 291 | Farrow & Ball · Modern Emulsion | матовая | 1 | 73 | 20,9 м² |
| | акцент А | | **К2** | Farrow & Ball No. 289 | Farrow & Ball · Modern Emulsion | матовая | 1 | 13 | 12,1 м² |
| | потолок | | **К3** | NCS S 0502-Y | Tikkurila · Anti-Reflex 2 | глубокомат. | 2 | 95 | 11,4 м² |
| | пол | | **КМ1** | по образцу | Coswick · Вековые традиции · арт. 1167-4250 | | | | 11,4 м² |
| | плинтус | | **К4** | Farrow & Ball No. 291 | МДФ · в цвет Farrow & Ball | | | 73 | 13,6 м |
| **9. Коридор** 6,02 м² | стены | | **К1** | Farrow & Ball No. 291 | Farrow & Ball · Modern Emulsion | матовая | 1 | 73 | 29,2 м² |
| | потолок | | **К3** | NCS S 0502-Y | Tikkurila · Anti-Reflex 2 | глубокомат. | 2 | 95 | 6,0 м² |
| | пол | | **КМ1** | по образцу | Coswick · Вековые традиции · арт. 1167-4250 | | | | 6,0 м² |
| | плинтус | | **К4** | Farrow & Ball No. 291 | МДФ · в цвет Farrow & Ball | | | 73 | 10,8 м |
| **10. Спальня мастер** 22,48 м² | стены | | **К1** | Farrow & Ball No. 291 | Farrow & Ball · Modern Emulsion | матовая | 1 | 73 | 31,5 м² |
| | акцент А | | **К2** | Farrow & Ball No. 289 | Farrow & Ball · Modern Emulsion | матовая | 1 | 13 | 12,1 м² |
| | потолок | | **К3** | NCS S 0502-Y | Tikkurila · Anti-Reflex 2 | глубокомат. | 2 | 95 | 22,5 м² |
| | пол | | **КМ1** | по образцу | Coswick · Вековые традиции · арт. 1167-4250 | | | | 22,5 м² |
| | плинтус | | **К4** | Farrow & Ball No. 291 | МДФ · в цвет Farrow & Ball | | | 73 | 18,5 м |
| **11. Ванная мастер** 2,13 м² | стены | | **КМ4** | Marvel Travertine | Atlas Concorde · арт. A8UZ | | | | 12,6 м² |
| | потолок | | **К9** | NCS S 0502-Y | Tikkurila · Luja 7 | матовая | 1 | 95 | 2,1 м² |
| | пол | | **КМ5** | по образцу | керамогранит · Atlas Concorde Marvel Travertine Sand Cross 60×60 Matte Sensitech, арт. AFUL (той же коллекции, что стены A8UZ; тон сверить по образцу) | | | | 2,1 м² |

## Условные обозначения

- **К1** — Farrow & Ball No. 291 · School House White — тёплый меловой белый · Modern Emulsion · матовая · кл. 1
- **К2** — Farrow & Ball No. 289 · Inchyra Blue — тёмный сине-серый · Modern Emulsion · матовая · кл. 1
- **К3** — NCS S 0502-Y · Белый с лёгкой желтизной · Tikkurila Anti-Reflex 2 · глубокомат. · кл. 2
- **К4** — Farrow & Ball No. 291 · School House White — тёплый меловой белый · МДФ
- **К5** — NCS S 0502-Y · Белый с лёгкой желтизной · Tikkurila Harmony · матовая · кл. 1
- **К6** — NCS S 0502-Y · Белый с лёгкой желтизной · МДФ
- **К7** — Farrow & Ball No. 255 · Tanner's Brown — тёмный шоколад · Modern Emulsion · матовая · кл. 1
- дерево (доска, паркет, ламинат) — рисунок досок
- керамогранит, плитка, камень — сетка швов по формату
- **К8** — Farrow & Ball No. 291 · School House White — тёплый меловой белый · МДФ · полуглянц. · кл. 2
- **К9** — NCS S 0502-Y · Белый с лёгкой желтизной · Tikkurila Luja 7 · матовая · кл. 1
- **КМ1** — инженерная доска · 1167-4250
- **КМ2** — керамогранит · A8UZ
- **КМ3** — аналог: керамогранит матовый, тон F497, 600×600×9 мм
- **КМ4** — плитка · A8UZ
- **КМ5** — керамогранит · Atlas Concorde Marvel Travertine Sand Cross 60×60 Matte Sensitech, арт. AFUL (той же коллекции, что стены A8UZ; тон сверить по образцу)

К — краска, КМ — отделочный материал (тон КМ — по описанию, эталон — образец материала); кл. — класс истирания (1 — самый стойкий к мытью); LRV — светлота цвета: 0 — чёрный, 100 — белый

## Перечень выкрасов на согласование

| № | Код | Бренд / веер | Пом. / стена | Подложка | Формат | Статус |
|---|---|---|---|---|---|---|
| 1 | No. 291 | Farrow & Ball | 1, 3, 4, 5, 8, 9, 10 | ГКЛ с грунтом; МДФ под эмаль | 600×1000; 300×600 | к выполнению |
| 2 | No. 289 | Farrow & Ball | 1 А, 8 А, 10 А | ГКЛ с грунтом | 600×1000 | к выполнению |
| 3 | S 0502-Y | NCS Tikkurila | 1, 2, 4, 6, 7, 8, 9, 10, 11 | ГКЛ с грунтом; МДФ под эмаль | 600×1000; 300×600 | к выполнению |
| 4 | No. 255 | Farrow & Ball | 3 А | ГКЛ с грунтом | 600×1000 | к выполнению |

**Допущения и предложения на листе**

Основа листа: размеры сняты со скана обмерного плана KV оформление (см): часть подписей не читается, помещения выровнены по читаемым размерам; контрольный обмер не выполнен (К-1); высота потолка 2650 мм принята по отметкам обмера (Н = 2,50…2,66 м, ригель 2,28 м) — уточнить при обмере (К-2); толщины стен 300 / 120 мм приняты, межквартирная стена и колонны — по скану, не замерены (К-1); разрешённая мощность 15 кВт принята по типовым ТУ; при объединении двух квартир — переоформление ТУ (К-4); подрайон климата не задан — принят не северный (жилые от 2,5 м) (К-8).

Знак «**» — предложение проектировщика, заказчиком не утверждено (согласовать с заказчиком): плинтус пом. 1–5, 7–10, акцент пом. 3, фартук пом. 5 — артикул изделия не выбран: позиция описана характеристиками («аналог по характеристикам»), артикул выбирается при закупке; пол пом. 6, 11 — пирог пола: стяжка 33 мм и обмазочная гидроизоляция добавлены разработчиком проекта; артикул изделия не выбран: позиция описана характеристиками («аналог по характеристикам»), артикул выбирается при закупке.

См. лист открытых вопросов (лист 6, записи К-1, К-2, К-4, К-8).

## Примечания

1. Цвет на листе и на экране — ориентир. До покраски — выкрас на объекте: не меньше А3 (или лист ГКЛ), на грунте под эту краску, не на белой шпаклёвке, в 2 слоя; на обороте — код, бренд, веер, дата. Смотреть днём и вечером, рядом с образцами пола и плитки; к основному цвету стен — ещё 2 соседних оттенка. Красить только в цвет утверждённого выкраса.
2. Краску заказывать по коду из графы «Система и код цвета» у бренда этого кода, не «аналогом» другого; весь объём одного кода — одной партией, колеруемую краску — за один проход машины.
3. Площади — те же, что в ведомости отделки (лист 54); сколько краски заказать — в спецификации отделочных материалов (лист 59).
4. Колерная карта на 2 листах: обозначения — на каждом, схема и палитра — на первом, выкрасы — на последнем.

| Изм. | Кол.уч | Лист | № док. | Подп. | Дата | | | |
|---|---|---|---|---|---|---|---|---|
| Разраб. | | Кырлан А.С. | | | 04.11.26 | **ГД-2026-009-АИ** | | |
| Пров. | | | | | | Квартира 103 м² | | |
| ГИП | | | | | | Общая площадь 100,72* м² · * размеры со скана, не замерены (реестр — л. 6, 7, К-1) | | |
| | | | | | | Дизайн-проект интерьера | Стадия: РП | Лист: 58 / Листов: 120 |
| Н. контр. | | | | | | **Колерная карта** М б/м | **Кырлан Александр Сергеевич** | |
| Утв. | | | | | | | | |

выпуск 04.11.2026 № 35b47f1c2a · стр. 65 из 130

# Спецификация отделочных материалов

**ПРЕДВАРИТЕЛЬНО · не для производства работ · открыто пунктов: 8 (реестр — л. 6, 7)**

Форма 1 по ГОСТ 21.110-2013 · количества — из геометрии проекта, с запасом · часть 1 из 2

| Поз. | Наименование и техническая характеристика | Тип, марка, обозначение документа | Код продукции | Поставщик | Ед. изм. | Кол. | Масса 1 ед., кг | Примечание |
|---|---|---|---|---|---|---|---|---|
| | **Лакокрасочные материалы** | | | | | | | |
| 1 | Краска интерьерная водно-дисперсионная акриловая для стен и потолков, матовая, класс мокрого истирания 1 по EN 13300, база A; цвет по вееру Farrow & Ball No. 291 «School House White — тёплый меловой белый», колеровка машинная | Farrow & Ball Modern Emulsion | | Farrow & Ball | л | 55 | | поз. К1 колерной карты; пом. 1, 3, 4, 5, 8, 9, 10; S = 206,3 м² × 2 сл. × 0,12 л/м² = 49,5 л, +10 % и 0,5 л на подкраску → ≥ 55,0 л; тара 11 × 5 л |
| 2 | Краска интерьерная водно-дисперсионная акриловая для акцентных стен, матовая, класс мокрого истирания 1 по EN 13300, база C; цвет по вееру Farrow & Ball No. 289 «Inchyra Blue — тёмный сине-серый», колеровка машинная | Farrow & Ball Modern Emulsion | | Farrow & Ball | л | 10 | | поз. К2 колерной карты; пом. 1, 8, 10; S = 35,6 м² × 2 сл. × 0,12 л/м² = 8,5 л, +10 % и 0,5 л на подкраску → ≥ 9,9 л; тара 2 × 5 л |
| 3 | Краска интерьерная водно-дисперсионная акриловая для потолков, глубокоматовая, класс мокрого истирания 2 по EN 13300, база A; цвет NCS S 0502-Y «Белый с лёгкой желтизной», колеровка машинная | Tikkurila Anti-Reflex 2 | | Tikkurila | л | 18,9 | | поз. К3 колерной карты; пом. 1, 2, 4, 7, 8, 9, 10; S = 67,8 м² × 2 сл. × 0,12 л/м² = 16,3 л, +10 % и 0,5 л на подкраску → ≥ 18,4 л; тара 2 × 9 л + 1 × 0,9 л |
| 4 | Краска интерьерная водно-дисперсионная акриловая для стен, матовая, класс мокрого истирания 1 по EN 13300, база A; цвет NCS S 0502-Y «Белый с лёгкой желтизной», колеровка машинная | Tikkurila Harmony | | Tikkurila | л | 9 | | поз. К5 колерной карты; пом. 2, 7; S = 29,5 м² × 2 сл. × 0,12 л/м² = 7,1 л, +10 % и 0,5 л на подкраску → ≥ 8,3 л; тара 1 × 9 л |
| 5 | Краска интерьерная водно-дисперсионная акриловая для акцентных стен, матовая, класс мокрого истирания 1 по EN 13300, база C; цвет по вееру Farrow & Ball No. 255 «Tanner's Brown — тёмный шоколад», колеровка машинная | Farrow & Ball Modern Emulsion | | Farrow & Ball | л | 7,5 | | поз. К7 колерной карты; пом. 3; S = 11,7 м² × 3 сл. × 0,12 л/м² = 4,2 л, +10 % и 0,5 л на подкраску → ≥ 5,1 л; тара 1 × 5 л + 1 × 2,5 л |
| 6 | Краска интерьерная водно-дисперсионная акриловая для потолков, матовая, класс мокрого истирания 1 по EN 13300, база A; цвет NCS S 0502-Y «Белый с лёгкой желтизной», колеровка машинная | Tikkurila Luja 7 | | Tikkurila | л | 2,7 | | поз. К9 колерной карты; пом. 6, 11; S = 6,0 м² × 2 сл. × 0,12 л/м² = 1,4 л, +10 % и 0,5 л на подкраску → ≥ 2,1 л; тара 1 × 2,7 л |
| 7 | Краска для МДФ и дерева в цвет Farrow & Ball No. 291 «School House White — тёплый меловой белый» — окраска плинтуса; блеск не ниже блеска стен | марка не задана | | | л | 2,4 | | поз. К4, К8; пом. 1, 3, 4, 5, 8, 9, 10; L = 92,6 м, S = 9,1 м² × 2 сл. × 0,12 л/м² + 10 %; продукт подобрать в веере Farrow & Ball |
| 8 | Краска для МДФ и дерева в цвет NCS S 0502-Y «Белый с лёгкой желтизной» — окраска плинтуса; блеск не ниже блеска стен | марка не задана | | | л | 0,5 | | поз. К6; пом. 2, 7; L = 10,8 м, S = 1,1 м² × 2 сл. × 0,12 л/м² + 10 %; продукт подобрать в веере NCS |
| 9 | Грунтовка акриловая под окраску стен и потолков — из системы производителя краски | по системе краски | | | м² | 357 | | площадь окраски стен, акцентов и потолков; 1 слой перед окраской; расход — по ТУ грунтовки |

**Допущения и предложения на листе**

Основа листа: размеры сняты со скана обмерного плана KV оформление (см): часть подписей не читается, помещения выровнены по читаемым размерам; контрольный обмер не выполнен (К-1); высота потолка 2650 мм принята по отметкам обмера (Н = 2,50…2,66 м, ригель 2,28 м) — уточнить при обмере (К-2); толщины стен 300 / 120 мм приняты, межквартирная стена и колонны — по скану, не замерены (К-1); разрешённая мощность 15 кВт принята по типовым ТУ; при объединении двух квартир — переоформление ТУ (К-4); подрайон климата не задан — принят не северный (жилые от 2,5 м) (К-8).

Знак «**» — предложение проектировщика, заказчиком не утверждено (согласовать с заказчиком): плинтус пом. 1–5, 7–10, акцент пом. 3, фартук пом. 5 — артикул изделия не выбран: позиция описана характеристиками («аналог по характеристикам»), артикул выбирается при закупке; пол пом. 6, 11 — пирог пола: стяжка 33 мм и обмазочная гидроизоляция добавлены разработчиком проекта; артикул изделия не выбран: позиция описана характеристиками («аналог по характеристикам»), артикул выбирается при закупке.

Изменения по листу без подписи: ИЗ-1.

См. лист открытых вопросов (лист 6, записи ИЗ-1, К-1, К-2, К-4, К-8).

| Изм. | Кол.уч | Лист | № док. | Подп. | Дата |
|---|---|---|---|---|---|
| Разраб. | | Кырлан А.С. | | | 04.11.26 |
| Пров. | | | | | |
| ГИП | | | | | |
| | | | | | |
| Н. контр. | | | | | |
| Утв. | | | | | |

**ГД-2026-009-АИ**

Квартира 103 м²

Общая площадь 100,72* м² · * размеры со скана, не замерены (реестр — л. 6, 7, К-1)

Дизайн-проект интерьера

| Стадия | Лист | Листов |
|---|---|---|
| РП | 59 | 120 |

**Спецификация отделочных материалов**

М б/м

**Кырлан Александр Сергеевич**

# Спецификация отделочных материалов

**ПРЕДВАРИТЕЛЬНО · не для производства работ · открыто пунктов: 8 (реестр — л. 6, 7)**

Форма 1 по ГОСТ 21.110-2013 · количества — из геометрии проекта, с запасом · часть 2 из 2

| Поз. | Наименование и техническая характеристика | Тип, марка, обозначение документа | Код продукции | Поставщик | Ед. изм. | Кол. | Масса 1 ед., кг | Примечание |
|---|---|---|---|---|---|---|---|---|
| | **Плитка и керамогранит** | | | | | | | |
| 10 | Atlas Concorde Marvel Travertine Sand Cross 60×60 Matte Sensitech, арт. AFUL (той же коллекции, что стены A8UZ; тон сверить по образцу), 600×600×9 мм, ректификат, водопоглощение 0,1 % (BIa), противоскольжение R10, PEI IV | Atlas Concorde Marvel Travertine Sand Cross 60×60 Matte Sensitech, арт. AFUL (той же коллекции, что стены A8UZ; тон сверить по образцу) | | | м² | 9,36 | | шов 2 мм; Ванная, пол; Ванная мастер, пол; по раскладке 23 шт (S = 6,04 м²), с запасом 26 шт |
| 11 | A8UZ, 600×1200×9 мм, ректификат, водопоглощение 0,1 % (BIa), противоскольжение R10, PEI IV | A8UZ | | Atlas Concorde | м² | 70,56 | | шов 2 мм; Ванная, стены А–Г; Ванная, короб инсталляции; Ванная мастер, стены А–Г; Ванная мастер, короб инсталляции; Прихожая-холл, пол; по раскладке 86 шт (S = 45,03 м²), с запасом 98 шт |
| 12 | Керамогранит матовый, тон F497, ректификат, водопоглощение 0,5 % (BIa) | аналог по характеристикам | | | м² | 2,22 | | 5. Кухня, фартук; раскладка не выполнена — S = 2,01 м² + 10 %; клей и затирка — по раскладке |
| | **Напольные покрытия** | | | | | | | |
| 13 | 1167-4250, рабочий слой 4 мм, эмиссия E1, укладка на клей | 1167-4250 | | Coswick | м² | 87,5 | | пом. 1, 2, 3, 5, 7, 8, 9, 10; S = 81,77 м² + 7 % (прямая укладка); к заказу — кратно упаковке |
| 14 | Клей для паркета и инженерной доски, эластичный (СМП / полиуретановый) | по рекомендации производителя доски | | | м² | 82 | | площадь приклейки; расход и шпатель — по ТУ клея |
| | **Погонажные изделия** | | | | | | | |
| 15 | Ultrawood Base 5340, ЛДФ под окраску, 83×15 мм, 2440 мм (арт. LDF-BASE-5340), крепление к стене, окраска в цвет Farrow & Ball No. 291 | Ultrawood Base 5340, ЛДФ под окраску, 83×15 мм, 2440 мм (арт. LDF-BASE-5340) | | | м | 102 | | пом. 1, 3, 4, 5, 8, 9, 10; L = 92,6 м (периметр без дверных проёмов) + 10 % на подрезку; в штуках — по длине планки |
| 16 | Ultrawood Base 5340, ЛДФ под окраску, 83×15 мм, 2440 мм (арт. LDF-BASE-5340), крепление к стене, окраска в цвет NCS S 0502-Y | Ultrawood Base 5340, ЛДФ под окраску, 83×15 мм, 2440 мм (арт. LDF-BASE-5340) | | | м | 12 | | пом. 2, 7; L = 10,8 м (периметр без дверных проёмов) + 10 % на подрезку; в штуках — по длине планки |
| | **Смеси и материалы для облицовки** | | | | | | | |
| 17 | Затирка для швов плитки, класс CG2WA по EN 13888 | Mapei Ultracolor Plus 132 | | Mapei | кг | 4 | | по раскладке (a+b)/(a·b) × шов × t × 1,6 + 10 %; в т. ч. 1,0 кг — позиции раскладки без марки |
| 18 | Клей плиточный C2 TE S1 по EN 12004, слой 5 мм | Ceresit CM 17 | | Ceresit | кг | 402 | | 17 меш. по 25 кг; 1,5 кг/м² на 1 мм слоя + 10 %; в т. ч. 105 кг — позиции раскладки без марки |
| 19 | Гидроизоляция обмазочная мокрых зон: пол, стены по периметру, зоны замачивания; 2 слоя с армирующей лентой в углах | аналог по характеристикам | | | м² | 18,7 | | площадь по листу раскладки плитки + 10 %; расход смеси — по ТУ |
| 20 | Лента демпферная по периметру пола из плитки | аналог по характеристикам | | | м | 27,1 | | периметр без дверных проёмов + 10 % |

## Примечания

1. Количества — из геометрии проекта: площади поверхностей по чистым граням стен до отделки (те же, что в ведомости отделки и колерной карте), плитка, клей и затирка — по раскладке плиточника; в графе «Кол.» — к заказу, с запасом.
2. Краска: расход 0,12 л/м² на слой в 2 слоя, если по ТУ не задан иной; запас 10 % и 0,5 л на подкраску каждого кода. Один код — одна партия, колеровка машинная в колеровочном центре бренда; в заказ — только после утверждения выкраса (колерная карта). Фасовка — по каталогу бренда на дату выпуска; к заказу — не меньше расчётного объёма.
3. «Аналог по характеристикам» — допускается изделие другого производителя с характеристиками не ниже указанных, по согласованию с автором проекта.
4. Графы «Код продукции» и «Масса 1 ед.» не заполнены: коды по классификатору продукции не присвоены, масса единицы до 25 кг (ГОСТ 21.110-2013).
5. Грунтовка и клей для доски указаны площадью обработки; объём — по ТУ выбранного продукта.

**Допущения и предложения на листе**

Основа листа: размеры сняты со скана обмерного плана KV оформление (см): часть подписей не читается, помещения выровнены по читаемым размерам; контрольный обмер не выполнен (К-1); высота потолка 2650 мм принята по отметкам обмера (Н = 2,50…2,66 м, ригель 2,28 м) — уточнить при обмере (К-2); толщины стен 300 / 120 мм приняты, межквартирная стена и колонны — по скану, не замерены (К-1); разрешённая мощность 15 кВт принята по типовым ТУ; при объединении двух квартир — переоформление ТУ (К-4); подрайон климата не задан — принят не северный (жилые от 2,5 м) (К-8).

Знак «**» — предложение проектировщика, заказчиком не утверждено (согласовать с заказчиком): плинтус пом. 1–5, 7–10, акцент пом. 3, фартук пом. 5 — артикул изделия не выбран: позиция описана характеристиками («аналог по характеристикам»), артикул выбирается при закупке; пол пом. 6, 11 — пирог пола: стяжка 33 мм и обмазочная гидроизоляция добавлены разработчиком проекта; артикул изделия не выбран: позиция описана характеристиками («аналог по характеристикам»), артикул выбирается при закупке.

См. лист открытых вопросов (лист 6, записи К-1, К-2, К-4, К-8).

| Изм. | Кол.уч | Лист | № док. | Подп. | Дата |
|---|---|---|---|---|---|
| Разраб. | | Кырлан А.С. | | | 04.11.26 |
| Пров. | | | | | |
| ГИП | | | | | |
| | | | | | |
| Н. контр. | | | | | |
| Утв. | | | | | |

**ГД-2026-009-АИ**

Квартира 103 м²

Общая площадь 100,72* м² · * размеры со скана, не замерены (реестр — л. 6, 7, К-1)

| Дизайн-проект интерьера | Стадия | Лист | Листов |
|---|---|---|---|
| | РП | 60 | 120 |
| **Спецификация отделочных материалов** М б/м | **Кырлан Александр Сергеевич** | | |

# Концепция декора и визуализации

Мид-сенчури · ретро с авторской мебелью · визуализации, палитра, материалы, ключевые предметы



**Визуализация 1. Вид сверху (3D): планировка с мебелью, текстилем и декором**

Расстановка — по плану мебели (лист 19); шторы, ковры, картины и растения — по плану текстиля и декора (лист 62).

## Материалы и фактуры




**Дуб натуральный**
пол: пом. 1, 2, 3, 5, 7, 8, 9, 10; рамы ДК3, ДК4, ДК7



**Букле**
подушки: Т10, Т16



**Лён**
портьеры, подушки, рулонная: Т1, Т4, Т7, Т11, Т14, Т19, Т22

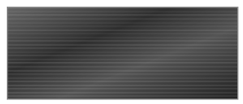

**Чёрный матовый металл**
рамы ДК5, ДК6 — чёрный



**Бархат**
подушки: Т5, Т17, Т23

## Ключевые предметы


— Диван Г2 2600×900 — гостиная-столовая; подушки и плед Т4, Т5, Т6
— Кровати М1, С1 — над изголовьем картины ДК4, ДК7; текстиль Т16, Т17, Т18, Т22, Т23, Т24
— Ковры Т3, Т9, Т15, Т21 — шерсть, на противоскользящей подложке
— Картины ДК1, ДК3, ДК4, ДК7 — центр на высоте 1450–1650 мм
— Зеркала в рост ДК5, ДК6
— Шторы-волна Т1, Т7, Т11, Т19 (NCS S 1005-Y20R), тюль Т2, Т8, Т13, Т20 (NCS S 0502-Y) — в нишах потолка
— Растение ДК2, растение ДК9

## Настроение

Ретро 2026: модернизм середины века 65 % + ар-деко 35 %. Стены — School House White No. 291, потолки — белый S 0502-Y; второй план — орех и тик, оливковый Bancha No. 298, сине-серый Inchyra Blue No. 289; акценты — горчица S 2050-Y20R, терракота S 3050-Y70R, тил S 5030-B10G, изумрудный бархат S 5040-B90G; металл — латунь. Мебель — авторские модели середины века (как предложение, модели уточняются с заказчиком). Настроение стиля: оптимизм, функциональность, тёплое дерево, лёгкость, ретро без китча, связь с улицей, графичные акценты. Свет тёплый, 2700–3000 K.

## Примечания


1. Визуализации — образ интерьера. Изделия, размеры, высоты подвеса и привязки — по чертежам (план текстиля и декора — лист 62; шторы и карнизы — лист 63; ведомость текстиля — лист 64; ведомость декора и развеска — лист 65); при расхождении действуют чертежи и ведомости.
2. Коды цвета — ориентир подбора по веерам производителей; ткань утверждается по образцу при дневном свете и при свете проекта 2700–3000 K.
3. Мелкий стайлинг на визуализациях (книги, посуда, свечи) в ведомости не входит и поставляется заказчиком по желанию.

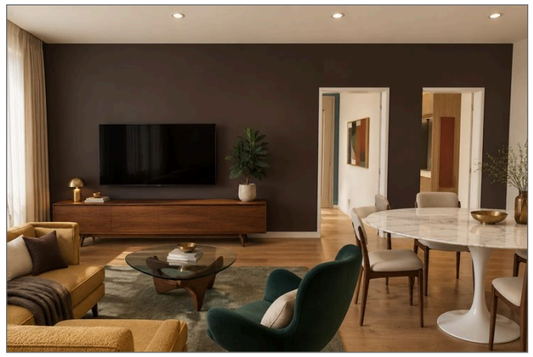

**Визуализация 18. Гостиная-столовая (пом. 3)**
шторы Т1, Т2 · ковёр Т3 · картина ДК1 · растение ДК2 · подушки, пледы Т4, Т5, Т6



**Визуализация 16. Кухня (пом. 5)**
шторы Т14 · растение ДК9

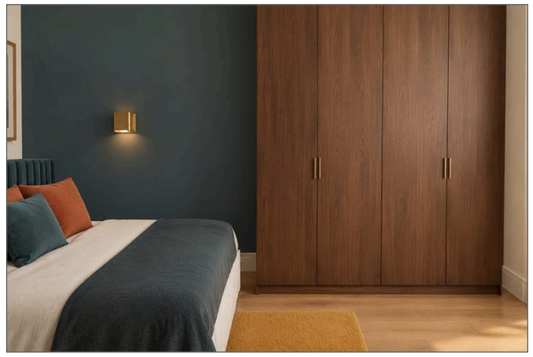

**Визуализация 6. Спальня 2 (пом. 8)**
шторы Т11, Т13 · ковёр Т15 · картина ДК4 · зеркало ДК6 · подушки, пледы Т16, Т17, Т18



**Визуализация 9. Спальня мастер (пом. 10)**
шторы Т19, Т20 · ковёр Т21 · картина ДК7 · подушки, пледы Т22, Т23, Т24

## Палитра 60/30/10 и цвета текстиля




- Farrow & Ball No. 291 (School House White — тёплый меловой белый), LRV 73 — 60 % база — Т2
- NCS S 0502-Y (Белый с лёгкой желтизной), LRV 95 — 60 % база — Т8, Т13, Т20
- Farrow & Ball No. 298 (Bancha — оливковый середины века), LRV 14 — 30 % второй цвет — Т3, Т21
- Farrow & Ball No. 289 (Inchyra Blue — тёмный сине-серый), LRV 13 — 30 % второй цвет — Т12, Т18, Т23, Т24
- Farrow & Ball No. 255 (Tanner's Brown — тёмный шоколад), LRV 7 — 30 % второй цвет — Т5, Т6
- NCS S 2050-Y20R (Горчичный), LRV 42 — 10 % акцент — Т9, Т15
- NCS S 3050-Y70R (Терракотовый / жжёный оранжевый), LRV 18 — 10 % акцент — Т10, Т16
- NCS S 5030-B10G (Тил), LRV 12 — 10 % акцент — Т17
- NCS S 5040-B90G (Изумрудный), LRV 8 — 10 % акцент
- NCS S 1005-Y20R (Светлый кремовый), LRV 77 — текстиль — Т1, Т4, Т7, Т11, Т14, Т19, Т22

Допущения и предложения на листе. Основа листа: размеры сняты со скана обмерного плана KV оформление (см): часть подписей не читается, помещения выровнены по читаемым размерам; контрольный обмер не выполнен (К-1); высота потолка 2650 мм принята по отметкам обмера (Н = 2,50…2,66 м, ригель 2,28 м) — уточнить при обмере (К-2); толщины стен 300 / 120 мм приняты, межквартирная стена и колонны — по скану, не замерены (К-1); разрешённая мощность 15 кВт принята по типовым ТУ; при объединении двух квартир — переоформление ТУ (К-4); подрайон климата не задан — принят не северный (жилые от 2,5 м) (К-8). См. лист открытых вопросов (лист 6, записи К-1, К-2, К-4, К-8).


| | | | | | | | | | |
|---|---|---|---|---|---|---|---|---|---|
| | | | | | | **ГД-2026-009-АИ** | | | |
| | | | | | | Квартира 103 м² | | | |
| Изм. | Кол.уч | Лист | № док. | Подп. | Дата | Общая площадь 100,72* м² · * размеры со скана, не замерены (реестр — л. 6, 7, К-1) | | | |
| Разраб. | | Кырлан А.С. | | | 04.11.26 | Дизайн-проект интерьера | Стадия | Лист | Листов |
| Пров. | | | | | | | РП | 61 | 120 |
| ГИП | | | | | | | | | |
| | | | | | | **Концепция декора и визуализации** | **Кырлан Александр Сергеевич** | | |
| Н. контр. | | | | | | М б/м | | | |
| Утв. | | | | | | | | | |

выпуск 04.11.2026 № 35b47f1c2a · стр. 68 из 130

# План текстиля и декора

Шторы и карнизы, ковры, картины и зеркала, растения · размеры в мм от чистовых стен и чистого пола · марки — по ведомостям

**ПРЕДВАРИТЕЛЬНО · не для производства работ · открыто пунктов: 8 (реестр — л. 6, 7)**

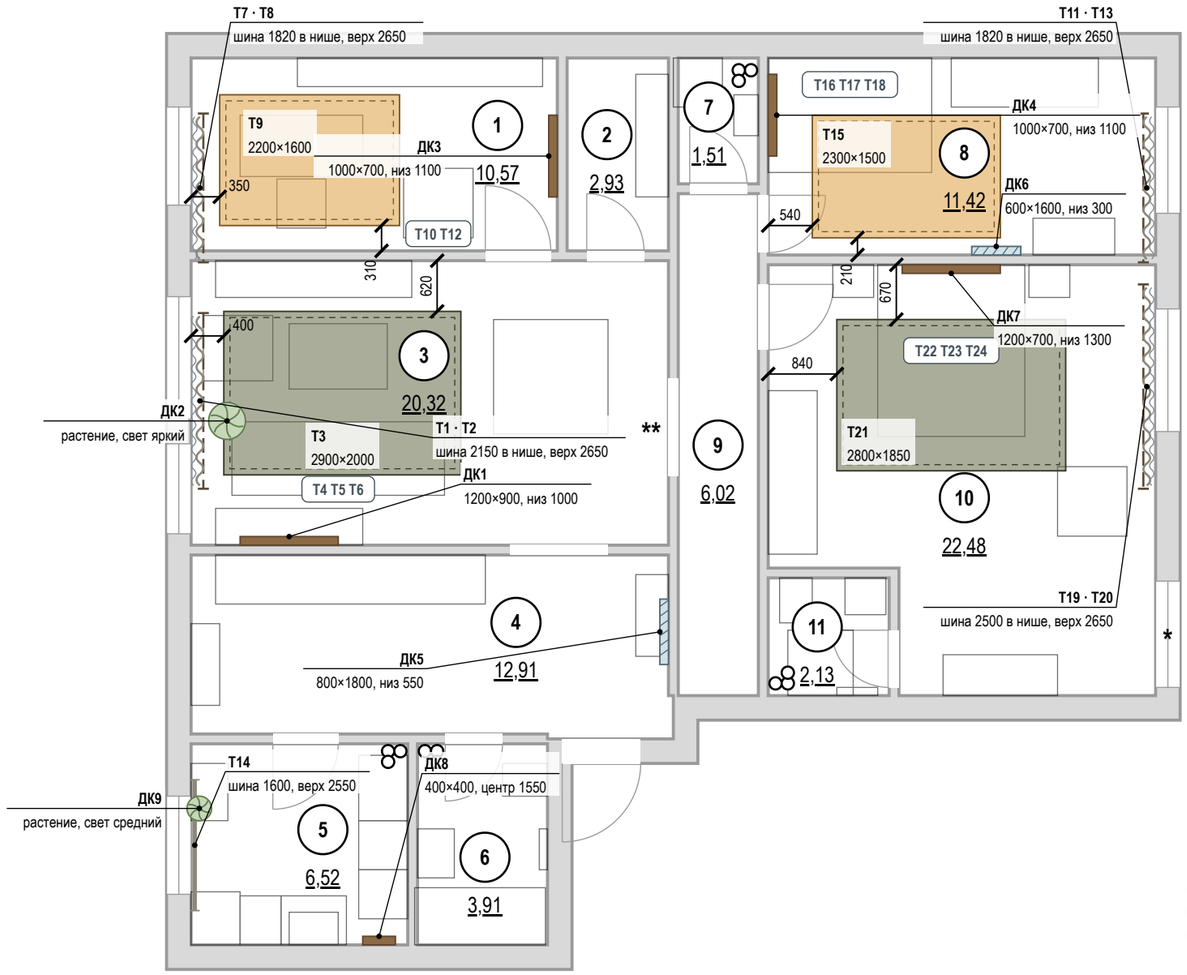


## Условные обозначения

- ковёр — габарит в масштабе, цвет изделия
- шина или карниз штор (выше плоскости разреза)
- портьеры (штора-волна)
- тюль (на плане — волнистая линия)
- римская или рулонная штора в проёме
- картина на стене — ширина в масштабе
- зеркало на стене — ширина в масштабе
- растение в кашпо — диаметр в масштабе
- ваза, настольный декор
- подушки, пледы — марки на мебели
- привязка от чистовой стены, мм
- (1) номер помещения, площадь м²
- стены (подложка обмера)
- * «*» — принято, не замерено и не подтверждено
- ** «**» — предложение проектировщика, заказчиком не утверждено

Т1, ДК1 — марки по ведомостям текстиля и декора

**Экспликация помещений**

лист 14 · на плане — номера в марках

## Окна: шина → полотно, мм

| Поз. | Шина | Верх шины | Полотно, низ |
|---|---|---|---|
| Т7, Т8 | 1820 | 2650, ниша | 2640, низ 10 |
| Т1, Т2 | 2150 | 2650, ниша | 2640, низ 10 |
| Т14 | 1600 | 2550 | 1750, низ 800 |
| Т11, Т13 | 1820 | 2650, ниша | 2640, низ 10 |
| Т19, Т20 | 2500 | 2650, ниша | 2640, низ 10 |

**Допущения и предложения на листе**

Основа листа: размеры сняты со скана обмерного плана KV оформление (см): часть подписей не читается, помещения выровнены по читаемым размерам; контрольный обмер не выполнен (К-1); высота потолка 2650 мм принята по отметкам обмера (Н = 2,50…2,66 м, ригель 2,28 м) — уточнить при обмере (К-2); толщины стен 300 / 120 мм приняты, межквартирная стена и колонны — по скану, не замерены (К-1); разрешённая мощность 15 кВт принята по типовым ТУ; при объединении двух квартир — переоформление ТУ (К-4); подрайон климата не задан — принят не северный (жилые от 2,5 м) (К-8).

Знак «*» — принято, не замерено и не подтверждено (замерить на объекте): К-1: окно пом. 10 (стена Б) — Окно 1300 при смещение 3500 на стене Б основной части (длина 3830) выходило за стену на 970 мм; К-6: Ст К1-3, Ст В1-3, Ст Т3-3 — положение снято со скана обмера, отдельно не замерялось; ось внутри габарита поддона См1 — обмер угла по К-6.

Знак «**» — предложение проектировщика, заказчиком не утверждено (согласовать с заказчиком): К-5: дверь пом. 3 (стена Б) — проём в межквартирной стене — объединение квартир, предложение до техзаключения.

См. лист открытых вопросов (лист 6, записи К-1, К-2, К-4–К-6, К-8).

## Примечания

1. Размеры — в мм. Отступы ковров — от чистовых стен; высоты картин и зеркал — от чистого пола до центра или низа рамы.
2. Шторы — на шинах в нишах потолка (ниша — план потолков, лист 45); закладная под шину — до обшивки ГКЛ. Схемы окон, длины полотен и сборка — лист 63.
3. Картины и зеркала массой более 5 кг — на анкеры по основанию, нагрузка крепежа не меньше двойной массы изделия; на ГКЛ — только по закладной. Декор не перекрывает розетки и выключатели.
4. Ковры на гладком полу — на противоскользящей подложке.
5. Мебель — по плану расстановки мебели (лист 19); ведомость текстиля — лист 64, ведомость декора и схемы развески — лист 65.
6. Знак «*» у проёма — допущение: положение проёма не замерено (окно пом. 10, стена Б); размер напечатан как принятый. Реестр: листы 6–7, вопрос К-1.
7. Номера помещений — по экспликации (лист 14); наименования и площади на этом листе не дублируются.
8. Марки текстиля «Т» и декора «Д» относятся только к листам текстиля и декора; индексы трубопроводов Т1–Т4 — на листах ВК и ОВ.

1000 мм · печать 1:1

| Изм. | Кол.уч | Лист | № док. | Подп. | Дата |
|---|---|---|---|---|---|
| Разраб. | | Кырлан А.С. | | | 04.11.26 |
| Пров. | | | | | |
| ГИП | | | | | |
| | | | | | |
| Н. контр. | | | | | |
| Утв. | | | | | |

**ГД-2026-009-АИ**

Квартира 103 м²

Общая площадь 100,72* м² · * размеры со скана, не замерены (реестр — л. 6, 7, К-1)

Дизайн-проект интерьера

| Стадия | Лист | Листов |
|---|---|---|
| РП | 62 | 120 |

**План текстиля и декора**

М 1:75

**Кырлан Александр Сергеевич**

выпуск 04.11.2026 № 35b47f1c2a · стр. 69 из 130

08

# Декор и текстиль


Кырлан Александр Сергеевич

выпуск 04.11.2026 · 35b47f1c2a · стр. 70 из 130


# Шторы и карнизы

Схемы окон «шина → полотно» (М 1:100) · отметки от чистого пола помещения · размеры в мм


**Окно 1 — Кабинет-библиотека (пом. 1): Т7, Т8 (М 1:100)**

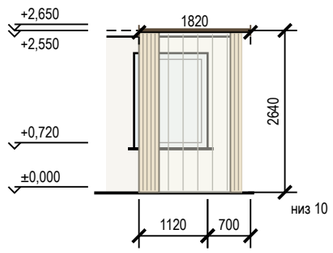



**Окно 1 — Гостиная-столовая (пом. 3): Т1, Т2 (М 1:100)**

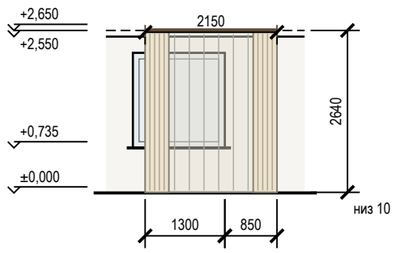



**Окно 1 — Кухня (пом. 5): Т14 (М 1:100)**

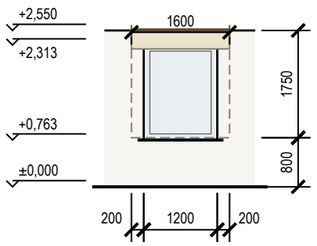


**Окно 1 — Спальня 2 (пом. 8): Т11, Т13 (М 1:100)**

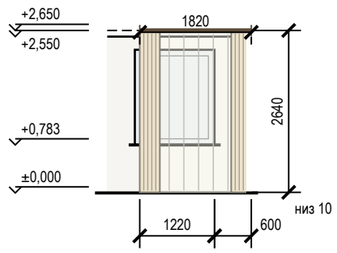


**Окно 1 — Спальня мастер (пом. 10): Т19, Т20 (М 1:100)**

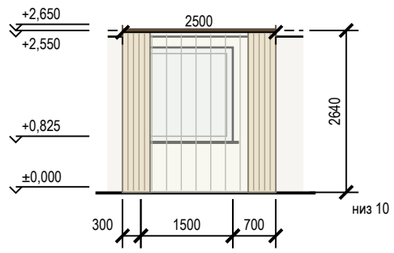


## Карта окон: окно → шина → полотно

| Поз. | Окно, пом. | Проём Ш×В, подоконник | Верх ниши | Изделие | Шина / карниз: длина, крепление | Верх шины | Полотно: длина, низ | Управление |
|---|---|---|---|---|---|---|---|---|
| Т7 | 1, пом. 1 | 1200×1560, подок. 720 | +2,650 | портьеры | шина, 1820, в нише потолка, вынос 150 | +2,650 | 2640, низ 10 (парит) | вручную |
| Т8 | 1, пом. 1 | 1200×1560, подок. 720 | +2,650 | тюль | шина, 1820, в нише потолка, вынос 150 | +2,650 | 2640, низ 10 (парит) | вручную |
| Т1 | 1, пом. 3 | 1500×1550, подок. 735 | +2,650 | портьеры | шина, 2150, в нише потолка, вынос 150 | +2,650 | 2640, низ 10 (парит) | вручную |
| Т2 | 1, пом. 3 | 1500×1550, подок. 735 | +2,650 | тюль | шина, 2150, в нише потолка, вынос 100 | +2,650 | 2640, низ 10 (парит) | вручную |
| Т14 | 1, пом. 5 | 1200×1550, подок. 763 | | рулонная штора | шина, 1600, на потолок, вынос 120 | +2,550 | 1750, низ 800 | без шнура |
| Т11 | 1, пом. 8 | 1300×1552, подок. 783 | +2,650 | портьеры | шина, 1820, в нише потолка, вынос 150 | +2,650 | 2640, низ 10 (парит) | вручную |
| Т13 | 1, пом. 8 | 1300×1552, подок. 783 | +2,650 | тюль | шина, 1820, в нише потолка, вынос 150 | +2,650 | 2640, низ 10 (парит) | вручную |
| Т19 | 1, пом. 10 | 1500×1548, подок. 825 | +2,650 | портьеры | шина, 2500, в нише потолка, вынос 150 | +2,650 | 2640, низ 10 (парит) | вручную |
| Т20 | 1, пом. 10 | 1500×1548, подок. 825 | +2,650 | тюль | шина, 2500, в нише потолка, вынос 150 | +2,650 | 2640, низ 10 (парит) | вручную |

## Задания смежникам

| Кому | Задание | Пом. |
|---|---|---|
| Гипсокартонщик | окно 1 (1200×1560, Т7, Т8): ниша под шторы 150×100, верх +2,650; закладная под шину L 1820 по всей длине — до обшивки | 1 |
| Гипсокартонщик | окно 1 (1500×1550, Т1, Т2): ниша под шторы 150×100, верх +2,650; закладная под шину L 2150 по всей длине — до обшивки | 3 |
| Гипсокартонщик | окно 1 (1300×1552, Т11, Т13): ниша под шторы 150×100, верх +2,650; закладная под шину L 1820 по всей длине — до обшивки | 8 |
| Гипсокартонщик | окно 1 (1500×1548, Т19, Т20): ниша под шторы 150×100, верх +2,650; закладная под шину L 2500 по всей длине — до обшивки | 10 |
| Электрик | выводы под электрокарнизы не требуются (управление вручную) | |

## Условные обозначения

- портьеры в открытом положении
- римская штора: сложена / опущена
- верх ниши под шторы в потолке
- тюль (на виде окна — прозрачная плашка)
- шина или карниз на отметке верха
- оконный проём

**Допущения и предложения на листе**

Основа листа: размеры сняты со скана обмерного плана KV оформление (см): часть подписей не читается, помещения выровнены по читаемым размерам; контрольный обмер не выполнен (К-1); высота потолка 2650 мм принята по отметкам обмера (Н = 2,50…2,66 м, ригель 2,28 м) — уточнить при обмере (К-2); толщины стен 300 / 120 мм приняты, межквартирная стена и колонны — по скану, не замерены (К-1); разрешённая мощность 15 кВт принята по типовым ТУ; при объединении двух квартир — переоформление ТУ (К-4); подрайон климата не задан — принят не северный (жилые от 2,5 м) (К-8).

Знак «*» — принято, не замерено и не подтверждено (замерить на объекте): К-1: окно пом. 10 (стена Б) — Окно 1300 при смещение 3500 на стене Б основной части (длина 3830) выходило за стену на 970 мм.

Знак «**» — предложение проектировщика, заказчиком не утверждено (согласовать с заказчиком): К-5: дверь пом. 3 (стена Б) — проём в межквартирной стене — объединение квартир, предложение до техзаключения.

См. лист открытых вопросов (лист 6, записи К-1, К-2, К-4, К-5, К-8).

## Примечания

1. Отметки — от чистого пола помещения; размеры — мм.
2. Шины в нишах потолка: закладная (брус или профиль) по всей длине ниши — до обшивки ГКЛ; ниша и её отметка — узел ниши на плане потолков (лист 45).
3. Шина в нише — на отметке верха ниши (крепление к закладной в потолке ниши); длина полотна — от верха шины до чистого пола за вычетом зазора.
4. Полотно портьер «парит» над полом на 10 мм; сборка портьер — 2,0, тюля — 2,5 (ширина полотна — в ведомости текстиля).
5. Шнур римской шторы — с натяжителем, петля низом не ниже 1500 мм от пола (защита детей; EN 13120 — рекомендация).
6. Электрокарнизы не предусмотрены; при замене на электропривод — вывод кабеля в нише у края шины (задание электрику).
7. Марки изделий — по плану текстиля и декора (лист 62) и ведомости текстиля (лист 64).

| Изм. | Кол.уч | Лист | № док. | Подп. | Дата |
|---|---|---|---|---|---|
| Разраб. | | Кырлан А.С. | | | 04.11.26 |
| Пров. | | | | | |
| ГИП | | | | | |
| | | | | | |
| Н. контр. | | | | | |
| Утв. | | | | | |

**ГД-2026-009-АИ**

Квартира 103 м²

Общая площадь 100,72* м² · * размеры со скана, не замерены (реестр — л. 6, 7, К-1)

Дизайн-проект интерьера

| Стадия | Лист | Листов |
|---|---|---|
| РП | 63 | 120 |

**Шторы и карнизы**

М б/м

**Кырлан Александр Сергеевич**

выпуск 04.11.2026 № 35b47f1c2a · стр. 71 из 130

# Ведомость текстиля

Шторы, тюль, римские шторы, ковры, подушки и пледы · размеры в мм · марки — по плану текстиля и декора

## Текстиль: шторы, ковры, подушки, пледы

| Поз. | Пом. | Изделие | Размер, мм | Ткань, состав, плотность | Сборка, ширина полотна | | Цвет (система, код) | Кол. | Примечание |
|---|---|---|---|---|---|---|---|---|---|
| T1 | 3 | Портьеры-волна, два полотна | шина 2150 × полотно 2640 | лён 100 %; 280 г/м² | × 2, ширина 4300 | | NCS S 1005-Y20R (Светлый кремовый) | 2 | низ 10 (парит); в нише потолка; уход: химчистка; отпаривание на карнизе |
| T2 | 3 | Тюль-вуаль, одно полотно | шина 2150 × полотно 2640 | вуаль; полиэстер 100 %; 60 г/м² | × 2,5, ширина 5375 | | Farrow & Ball No. 291 (School House White тёплый меловой белый) | 1 | низ 10 (парит); в нише потолка; уход: стирка 30 °C, вешать влажной |
| T3 | 3 | Ковёр мягкой группы, абстрактная геометрия середины века | 2900×2000 | шерсть, плоское плетение; шерсть 100 % | | | Farrow & Ball No. 298 (Bancha — оливковый середины века) | 1 | противоскользящая подложка; ворс 8 мм; уход: сухая чистка, пылесос без турбощётки |
| T4 | 3 | Подушки декоративные на диван | 500×500 | лён 100 % | | | NCS S 1005-Y20R (Светлый кремовый) | 3 | на Г2; уход: съёмный чехол, стирка 30 °C |
| T5 | 3 | Подушки декоративные на диван, акцент | 400×600 | хлопковый бархат 100 % | | | Farrow & Ball No. 255 (Tanner's Brown — тёмный шоколад) | 2 | на Г2; уход: химчистка |
| T6 | 3 | Плед на диван | 1300×1700 | шерсть мериноса 100 % | | | Farrow & Ball No. 255 (Tanner's Brown — тёмный шоколад) | 1 | на Г2; уход: ручная стирка 30 °C |
| T7 | 1 | Портьеры-волна | шина 1820 × полотно 2640 | лён с блэкаут-подкладкой; лён 100 %; 320 г/м² | × 2, ширина 3640 | | NCS S 1005-Y20R (Светлый кремовый) | 2 | низ 10 (парит); в нише потолка |
| T8 | 1 | Тюль | шина 1820 × полотно 2640 | вуаль; полиэстер 100 % | × 2,5, ширина 4550 | | NCS S 0502-Y (Белый с лёгкой желтизной) | 1 | низ 10 (парит); в нише потолка |
| T9 | 1 | Ковёр под рабочей зоной, геометрия середины века | 2200×1600 | шерсть, плоское плетение; шерсть 100 % | | | NCS S 2050-Y20R (Горчичный) | 1 | противоскользящая подложка; ворс 8 мм |
| T10 | 1 | Подушки декоративные на кровать | 500×500 | букле (шерсть 60 %, полиэстер 40 %) | | | NCS S 3050-Y70R (Терракотовый / жжёный оранжевый) | 3 | на Б4 |
| T11 | 8 | Портьеры-волна | шина 1820 × полотно 2640 | лён с блэкаут-подкладкой; лён 100 %; 320 г/м² | × 2, ширина 3640 | | NCS S 1005-Y20R (Светлый кремовый) | 2 | низ 10 (парит); в нише потолка |
| T12 | 1 | Плед на кровать | 1300×1700 | шерсть мериноса 100 % | | | Farrow & Ball No. 289 (Inchyra Blue — тёмный сине-серый) | 1 | на Б4 |
| T13 | 8 | Тюль | шина 1820 × полотно 2640 | вуаль; полиэстер 100 % | × 2,5, ширина 4550 | | NCS S 0502-Y (Белый с лёгкой желтизной) | 1 | низ 10 (парит); в нише потолка |
| T14 | 5 | Рулонная штора кассетная, ткань димаут | шина 1600 × полотно 1750 | ткань димаут с грязеотталкивающей пропиткой; полиэстер 100 % | | | NCS S 1005-Y20R (Светлый кремовый) | 1 | низ 800; на потолок; шнур: петля —, cordless; уход: протирка влажной губкой |
| T15 | 8 | Ковёр под кроватью | 2300×1500 | шерсть, плоское плетение; шерсть 100 % | | | NCS S 2050-Y20R (Горчичный) | 1 | противоскользящая подложка; ворс 8 мм |
| T16 | 8 | Подушки декоративные на кровать | 500×500 | букле (шерсть 60 %, полиэстер 40 %) | | | NCS S 3050-Y70R (Терракотовый / жжёный оранжевый) | 3 | на С1 |
| T17 | 8 | Подушки на кровать, акцент | 400×600 | хлопковый бархат 100 % | | | NCS S 5030-B10G (Тил) | 2 | на С1 |
| T18 | 8 | Плед на кровать | 1300×1700 | шерсть мериноса 100 % | | | Farrow & Ball No. 289 (Inchyra Blue — тёмный сине-серый) | 1 | на С1 |
| T19 | 10 | Портьеры-волна | шина 2500 × полотно 2640 | лён с блэкаут-подкладкой; лён 100 %; 320 г/м² | × 2, ширина 5000 | | NCS S 1005-Y20R (Светлый кремовый) | 2 | низ 10 (парит); в нише потолка |
| T20 | 10 | Тюль | шина 2500 × полотно 2640 | вуаль; полиэстер 100 % | × 2,5, ширина 6250 | | NCS S 0502-Y (Белый с лёгкой желтизной) | 1 | низ 10 (парит); в нише потолка |
| T21 | 10 | Ковёр под кроватью | 2800×1850 | шерсть, ручное ткачество; шерсть 80 %, хлопок 20 % | | | Farrow & Ball No. 298 (Bancha — оливковый середины века) | 1 | противоскользящая подложка; ворс 10 мм |
| T22 | 10 | Подушки декоративные на кровать | 500×500 | лён 100 % | | | NCS S 1005-Y20R (Светлый кремовый) | 3 | на М1 |
| T23 | 10 | Подушки на кровать, акцент | 400×600 | хлопковый бархат 100 % | | | Farrow & Ball No. 289 (Inchyra Blue — тёмный сине-серый) | 2 | на М1 |
| T24 | 10 | Плед на кровать | 1300×1700 | шерсть мериноса 100 % | | | Farrow & Ball No. 289 (Inchyra Blue — тёмный сине-серый) | 1 | на М1 |

образец цвета — по HEX производителя краски, справочно

Итого: шторы и тюль — 13 шт.; ковры и дорожки — 4 шт.; подушки, пледы, покрывала — 22 шт.

## Примечания

1. Коды цвета — ориентир подбора по веерам производителей красок; ткань утверждается по образцу при дневном свете и при свете проекта 2700–3000 K.
2. Размеры полотен — по замеру после чистовой отделки пола и потолка; ширина полотна указана с учётом сборки, без припусков на швы. Схемы окон и отметки шин лист 63.
3. Портьеры и тюль — на тесьме «волна» по системе шины; блэкаут — подкладкой. Ковры — на противоскользящей подложке.
4. Замена изделия — аналогом по характеристикам (состав, плотность, размер, цвет по образцу) с согласованием автора проекта.
5. Места изделий — план текстиля и декора (лист 62); подушки и пледы — по марке мебели.

**Допущения и предложения на листе**

Основа листа: размеры сняты со скана обмерного плана KV оформление (см): часть подписей не читается, помещения выровнены по читаемым размерам; контрольный обмер не выполнен (К-1); высота потолка 2650 мм принята по отметкам обмера (Н = 2,50…2,66 м, ригель 2,28 м) — уточнить при обмере (К-2); толщины стен 300 / 120 мм приняты, межквартирная стена и колонны — по скану, не замерены (К-1); разрешённая мощность 15 кВт принята по типовым ТУ; при объединении двух квартир — переоформление ТУ (К-4); подрайон климата не задан — принят не северный (жилые от 2,5 м) (К-8).
См. лист открытых вопросов (лист 6, записи К-1, К-2, К-4, К-8).

| Изм. | Кол.уч | Лист | № док. | Подп. | Дата |
|---|---|---|---|---|---|
| Разраб. | | Кырлан А.С. | | | 04.11.26 |
| Пров. | | | | | |
| ГИП | | | | | |
| | | | | | |
| Н. контр. | | | | | |
| Утв. | | | | | |

**ГД-2026-009-АИ**

Квартира 103 м²

Общая площадь 100,72* м² · * размеры со скана, не замерены (реестр — л. 6, 7, К-1)

Дизайн-проект интерьера

| Стадия | Лист | Листов |
|---|---|---|
| РП | 64 | 120 |

**Ведомость текстиля**

М б/м

**Кырлан Александр Сергеевич**

выпуск 04.11.2026 № 35b47f1c2a · стр. 72 из 130

# Ведомость декора. Схемы развески

Картины, зеркала, растения, настольный декор · схемы развески (М 1:50) · высоты — мм от чистого пола


**ПРЕДВАРИТЕЛЬНО · не для производства работ · открыто пунктов: 8 (реестр — л. 6, 7)**

## Декор: картины, зеркала, растения, предметы


картина · зеркало · мебель под изделием

| Поз. | Пом. | Предмет | Размер, мм | Место: стена, высота от пола, мм | Масса, кг | Крепёж и основание | Свет места, отделка | Кол. |
|---|---|---|---|---|---|---|---|---|
| ДК1 | 3 | Картина над буфетом: Песочные и грейжевые поля, холст | 1200×900 | стена В, привязка 600; низ 1000, центр 1450; над Г6 | 6 | планка на дюбелях, 4 точки; основание: перегородка 120 мм; нагрузка 20 кг | | 1 |
| ДК2 | 3 | Фикус лировидный в кашпо Ø400 | 450×450 | напольное | | | свет яркий рассеянный | 1 |
| ДК3 | 1 | Картина над креслом: Горизонт над полем, карандаш | 1000×700 | стена Б, привязка 700; низ 1100, центр 1450; над Б4 | 4 | подвес по основанию, 2 точки | рама — дуб | 1 |
| ДК4 | 8 | Картина над кроватью: Горизонт над полем, карандаш | 1000×700 | стена Г, привязка 200; низ 1100, центр 1450; над С1 | 4 | подвес по основанию, 2 точки | рама — дуб | 1 |
| ДК5 | 4 | Зеркало | 800×1800 | стена Б, привязка 540; низ 550, центр 1450 | 18 | анкер, 4 шт.; основание: перегородка — определить обмером до монтажа; нагрузка 40 кг | рама — чёрный матовый металл | 1 |
| ДК6 | 8 | Зеркало в рост в тонкой чёрной раме | 600×1600 | стена В, привязка 2490; низ 300, центр 1100 | 12 | анкер для пустотелых оснований, 4 шт.; основание: перегородка — определить обмером до монтажа; нагрузка 30 кг | рама — чёрный матовый металл | 1 |
| ДК7 | 10 | Картина над кроватью: Серо-синяя абстракция, холст | 1200×700 | стена А, привязка 1640; низ 1300, центр 1650; над М1 | 4 | подвес по основанию, 2 точки | рама — дуб | 1 |
| ДК8 | 5 | Часы настенные Ø400 | 400×400 | стена В, привязка 2100; центр 1550 | 2 | дюбель с крюком, 1 точка; основание: перегородка 120 мм; нагрузка 10 кг | | 1 |
| ДК9 | 5 | Хлорофитум хохлатый на подоконнике (отм. +0,800) | 300×200 | напольное | | | свет средний | 1 |


**ДК1 — Гостиная-столовая (пом. 3), стена В (М 1:50)**

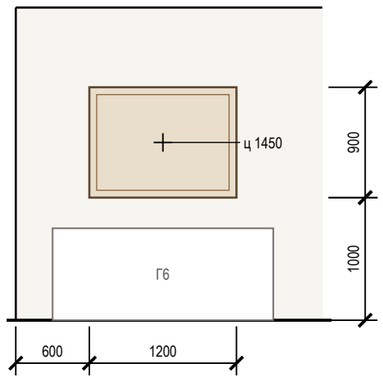



**ДК3 — Кабинет-библиотека (пом. 1), стена Б (М 1:50)**

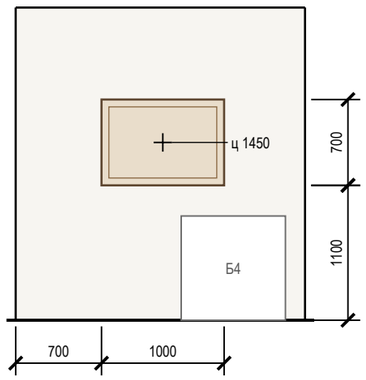



**ДК4 — Спальня 2 (пом. 8), стена Г (М 1:50)**

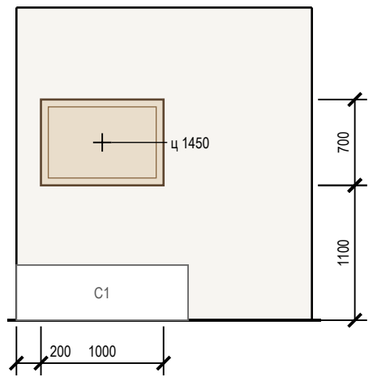



**ДК5 — Прихожая-холл (пом. 4), стена Б (М 1:50)**

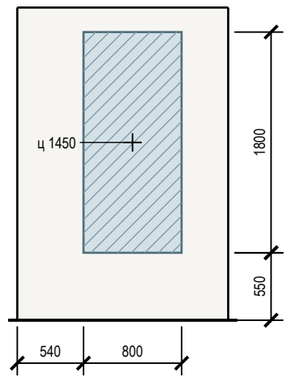



**ДК6 — Спальня 2 (пом. 8), стена В (М 1:50)**

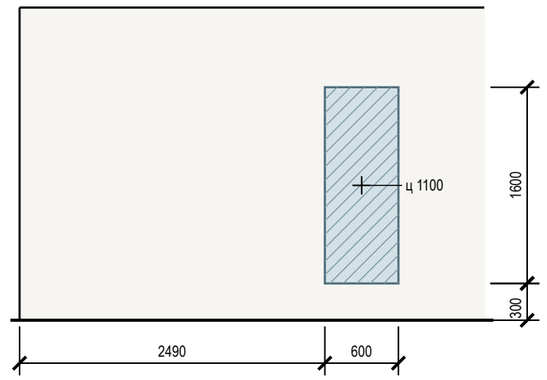


**ДК7 — Спальня мастер (пом. 10), стена А (М 1:50)**

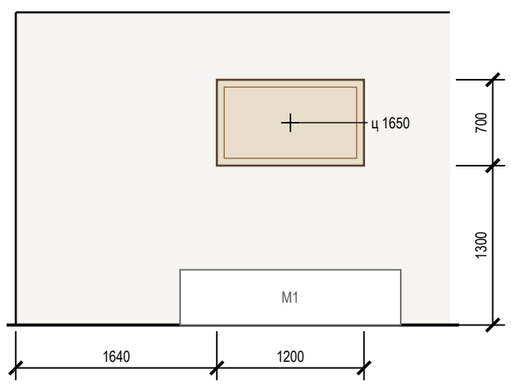


**ДК8 — Кухня (пом. 5), стена В (М 1:50)**

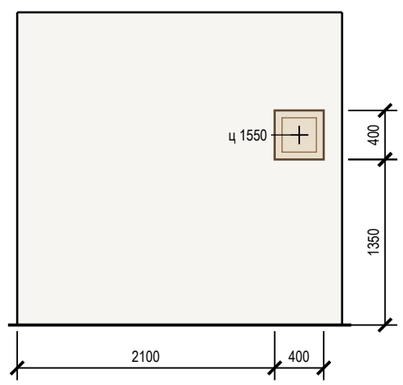


**Допущения и предложения на листе**

Основа листа: размеры сняты со скана обмерного плана KV оформление (см): часть подписей не читается, помещения выровнены по читаемым размерам; контрольный обмер не выполнен (К-1); высота потолка 2650 мм принята по отметкам обмера (Н = 2,50…2,66 м, ригель 2,28 м) — уточнить при обмере (К-2); толщины стен 300 / 120 мм приняты, межквартирная стена и колонны — по скану, не замерены (К-1); разрешённая мощность 15 кВт принята по типовым ТУ; при объединении двух квартир — переоформление ТУ (К-4); подрайон климата не задан — принят не северный (жилые от 2,5 м) (К-8).

См. лист открытых вопросов (лист 6, записи К-1, К-2, К-4, К-8).

## Примечания

1. Высоты — от чистого пола помещения до низа изделия, «ц» — до центра; привязки — от чистовой грани угла стены, мм.
2. Над мебелью низ изделия — на 150–250 мм выше спинки или изголовья; без мебели центр — на 1450–1600 мм от пола.
3. Изделия до 5 кг — на два подвеса по основанию; тяжелее — на анкеры с нагрузкой не меньше двойной массы; на ГКЛ — только по закладной или анкеру для пустотелых оснований.
4. Зеркала в рост — с креплением от опрокидывания; в санузлах — влагостойкие, на клей для зеркал и нейтральный силикон.
5. Места изделий — план текстиля и декора (лист 62).

| Изм. | Кол.уч | Лист | № док. | Подп. | Дата |
|---|---|---|---|---|---|
| Разраб. | | Кырлан А.С. | | | 04.11.26 |
| Пров. | | | | | |
| ГИП | | | | | |
| | | | | | |
| Н. контр. | | | | | |
| Утв. | | | | | |

**ГД-2026-009-АИ**

Квартира 103 м²

Общая площадь 100,72* м² · * размеры со скана, не замерены (реестр — л. 6, 7, К-1)

Дизайн-проект интерьера

| Стадия | Лист | Листов |
|---|---|---|
| РП | 65 | 120 |

**Ведомость декора. Схемы развески**

М б/м


**Кырлан Александр Сергеевич**

выпуск 04.11.2026 № 35b47f1c2a · стр. 73 из 130

# Встроенная мебель. Схема расположения

встроенная и корпусная мебель на заказ, кухонный гарнитур · размеры в мм · марки — по ведомости изделий

**ПРЕДВАРИТЕЛЬНО · не для производства работ · открыто пунктов: 8 (реестр — л. 6, 7)**

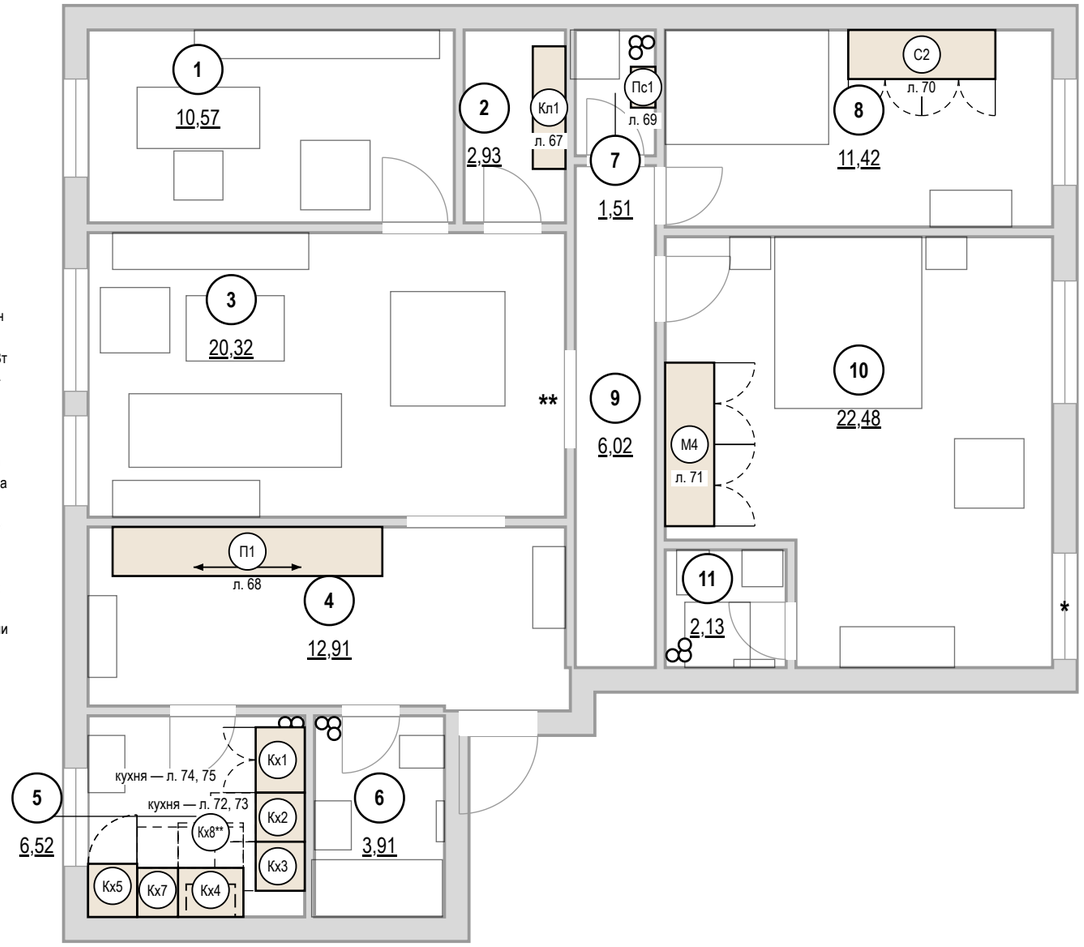


**Допущения и предложения на листе**

Основа листа: размеры сняты со скана обмерного плана KV оформление (см): часть подписей не читается, помещения выровнены по читаемым размерам; контрольный обмер не выполнен (К-1); высота потолка 2650 мм принята по отметкам обмера (Н = 2,50…2,66 м, ригель 2,28 м) — уточнить при обмере (К-2); толщины стен 300 / 120 мм приняты, межквартирная стена и колонны — по скану, не замерены (К-1); разрешённая мощность 15 кВт принята по типовым ТУ; при объединении двух квартир — переоформление ТУ (К-4); подрайон климата не задан — принят не северный (жилые от 2,5 м) (К-8).

Знак «*» — принято, не замерено и не подтверждено (замерить на объекте): К-1: окно пом. 10 (стена Б) — Окно 1300 при смещение 3500 на стене Б основной части (длина 3830) выходило за стену на 970 мм; К-6: Ст К1-3, Ст В1-3, Ст Т3-3 — положение снято со скана обмера, отдельно не замерялось; ось внутри габарита поддона См1 — обмер угла по К-6.

Знак «**» — предложение проектировщика, заказчиком не утверждено (согласовать с заказчиком): Кх8 — над индукционной панелью Кх4 нужна вытяжка: в составе кухни её не было, розетка вытяжки образца висела без потребителя; К-5: дверь пом. 3 (стена Б) — проём в межквартирной стене — объединение квартир, предложение до техзаключения.

См. лист открытых вопросов (лист 6, записи К-1, К-2, К-4–К-6, К-8).

## Ведомость изделий

| Марка | Наименование | Пом. | Ш×Г×В, мм | Лист |
|---|---|---|---|---|
| Кл1 | Система хранения | 2 | 1500×400×2400 | 67 |
| П1 | Шкаф-купе | 4 | 3300×600×2450 | 68 |
| Пс1 | Система хранения | 7 | 500×300×2000 | 69 |
| С2 | Шкаф распашной | 8 | 1800×600×2400 | 70 |
| М4 | Шкаф распашной | 10 | 2000×600×2400 | 71 |
| Кх1 | Модуль нижний: мойка | 5 | 800×600×900 | 72 |
| Кх2 | Модуль под ПММ 60: без корпуса, фасад на дверь машины | 5 | 600×600×900 | 72 |
| Кх3 | Модуль нижний: ящики | 5 | 600×600×900 | 72 |
| Кх4 | Модуль нижний: духовой шкаф, варочная | 5 | 800×600×900 | 74 |
| Кх8** | Модуль навесной: полки | 5 | 600×400×600 | 74 |
| Кх7 | Модуль нижний: ящики | 5 | 500×600×900 | 74 |
| Кх5 | Пенал: холодильник встр. | 5 | 600×650×2100 | 74 |

## Условные обозначения

- изделие мебельщика: корпус на полу
- невидимый контур: навесной модуль, корпус под столешницей
- открывание распашного фасада
- зона выдвижения ящика, двери техники
- дверь купе, стрелка — направление движения
- К1 — марка изделия или модуля (на схеме расположения под ней — лист изделия)
- * — «*» — принято, не замерено и не подтверждено
- ** — «**» — предложение проектировщика, заказчиком не утверждено

## Примечания

1. Изделия — по чистовым размерам помещений; перед раскроем — контрольный замер цеха после чистовой отделки стен, пола и потолка.
2. Открывание фасадов и выдвижение ящиков показано в открытом положении: зоны не пересекают двери, радиаторы, выключатели и проходы.
3. Стояки и счётчики за мебелью — с сервисным люком; газовые трубы мебелью не зашиваются.
4. Покупная мебель — по плану расстановки мебели и спецификации дизайнера; здесь — подложкой.
5. Знак «*» у проёма — положение не замерено; реестр: листы 6–7, вопрос К-1.

1000 мм · печать 1:1

| Изм. | Кол.уч | Лист | № док. | Подп. | Дата |
|---|---|---|---|---|---|
| Разраб. | | Кырлан А.С. | | | 04.11.26 |
| Пров. | | | | | |
| ГИП | | | | | |
| Н. контр. | | | | | |
| Утв. | | | | | |

**ГД-2026-009-АИ**

Квартира 103 м²

Общая площадь 100,72* м² · * размеры со скана, не замерены (реестр — л. 6, 7, К-1)

| Дизайн-проект интерьера | Стадия | Лист | Листов |
|---|---|---|---|
| | РП | 66 | 120 |

**Встроенная мебель. Схема расположения**

М 1:75


**Кырлан Александр Сергеевич**

# Система хранения Кл1


Кладовая (пом. 2) · вид из помещения · размеры в мм, отметки в м

ПРЕДВАРИТЕЛЬНО · не для производства работ · открыто пунктов: 8 (реестр — л. 6, 7)


**Общий вид**

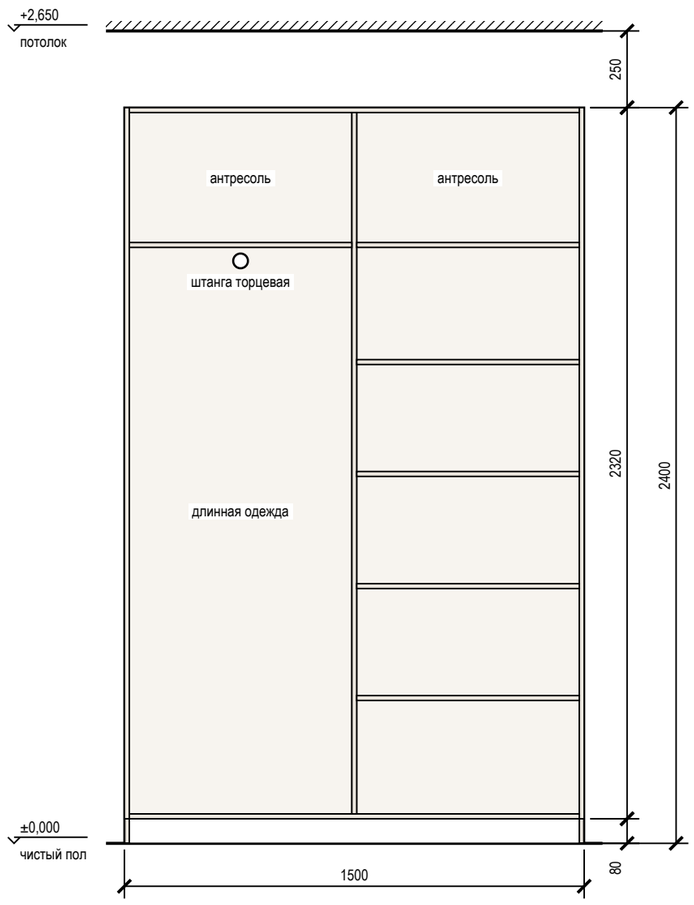



**Наполнение, размеры в свету**

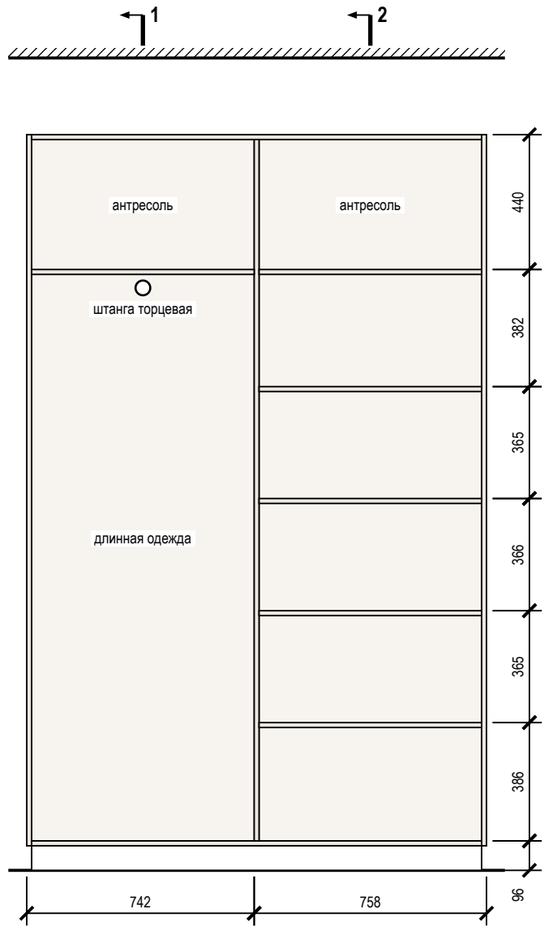


**Разрез 1-1**

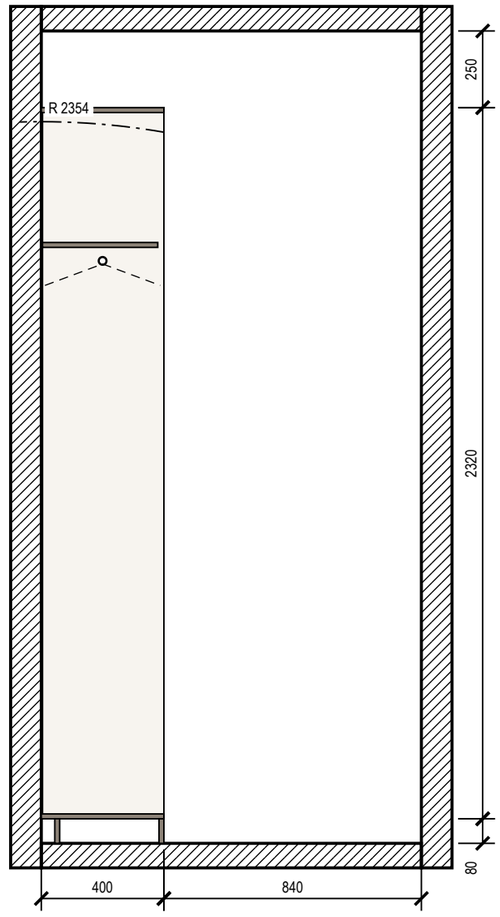


**Разрез 2-2**

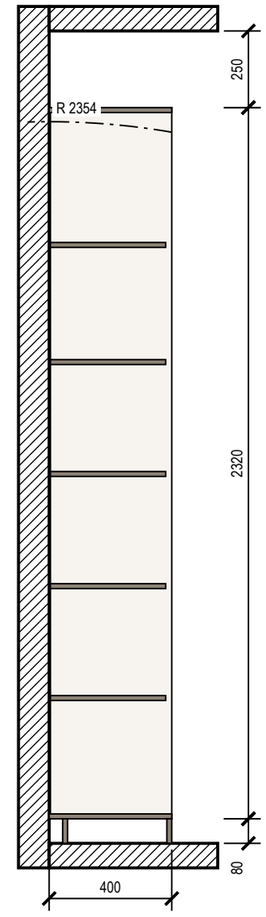


## Примечания

1. Размеры — в мм по чистовой отделке; изделие 1500×400×2400 (Ш×Г×В). Перед раскроем — контрольный замер цеха после чистовой отделки стен, пола и потолка.
2. Корпус — ЛДСП декор «орех» 16 мм, задняя стенка ХДФ 4 мм в паз, цоколь 80 мм на регулируемых опорах; открытая система: без фасадов.
3. Кромка: скрытые торцы 0,4 мм, видимые 2 мм (ПВХ/АБС).
4. Присадка по 32-й системе — выполняет цех.
5. Зазор до потолка 250 мм.
6. Подъём корпуса: диагональ боковины без цоколя $\sqrt{(2320^2 + 400^2)} = 2354$ мм < 2650 мм до потолка — корпус собирается лёжа, поднимается поворотом и ставится на цоколь.
7. Крепление к стене от опрокидывания — уголки 2 шт. к несущему основанию (монтажная схема шкафов).
8. Проход перед изделием 840 мм показан на разрезе 1-1.

## Условные обозначения

- корпус и полки ЛДСП (вид на стену)
- задняя стенка ХДФ
- деталь в разрезе
- штанга для плечиков (на разрезе — плечики 450 мм)
- траектория угла корпуса при подъёме в проектное положение

**Допущения и предложения на листе**

Основа листа: размеры сняты со скана обмерного плана KV оформление (см): часть подписей не читается, помещения выровнены по читаемым размерам; контрольный обмер не выполнен (К-1); высота потолка 2650 мм принята по отметкам обмера (Н = 2,50…2,66 м, ригель 2,28 м) — уточнить при обмере (К-2); толщины стен 300 / 120 мм приняты, межквартирная стена и колонны — по скану, не замерены (К-1); разрешённая мощность 15 кВт принята по типовым ТУ; при объединении двух квартир — переоформление ТУ (К-4); подрайон климата не задан — принят не северный (жилые от 2,5 м) (К-8).
См. лист открытых вопросов (лист 6, записи К-1, К-2, К-4, К-8).

1000 мм · печать 1:1

| Изм. | Кол.уч | Лист | № док. | Подп. | Дата |
|---|---|---|---|---|---|
| Разраб. | | Кырлан А.С. | | | 04.11.26 |
| Пров. | | | | | |
| ГИП | | | | | |
| | | | | | |
| Н. контр. | | | | | |
| Утв. | | | | | |

**ГД-2026-009-АИ**

Квартира 103 м²

Общая площадь 100,72* м² · * размеры со скана, не замерены (реестр — л. 6, 7, К-1)

Дизайн-проект интерьера

| Стадия | Лист | Листов |
|---|---|---|
| РП | 67 | 120 |

**Система хранения Кл1**

М 1:20

Кырлан Александр Сергеевич


выпуск 04.11.2026 № 35b47f1c2a · стр. 75 из 130

# Шкаф-купе П1


Прихожая-холл (пом. 4) · вид из помещения · размеры в мм, отметки в м

**ПРЕДВАРИТЕЛЬНО · не для производства работ · открыто пунктов: 8 (реестр — л. 6, 7)**


**Вид с фасадами**

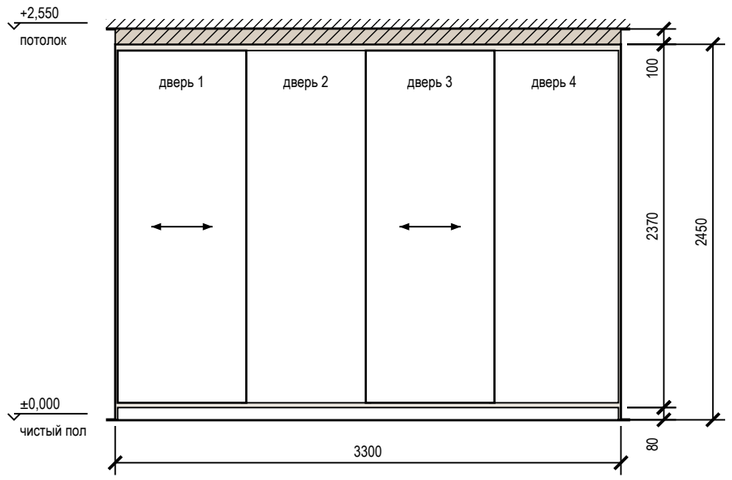



**Вид без фасадов**

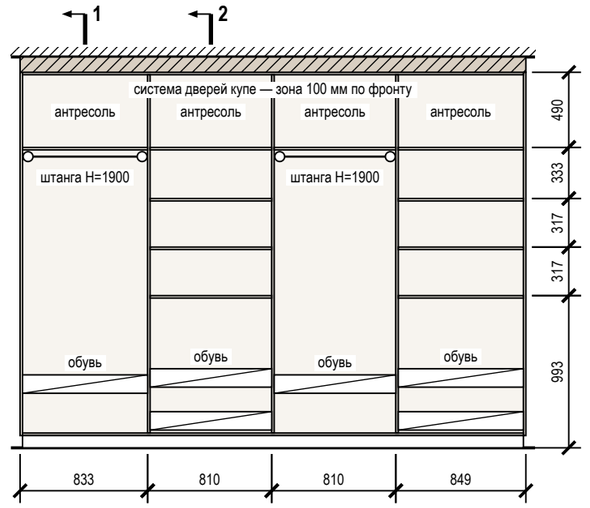


**Разрез 1-1**

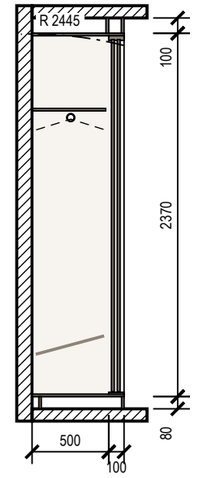


**Разрез 2-2**

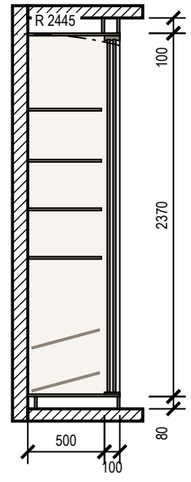


## Примечания

1. Размеры — в мм по чистовой отделке; изделие 3300×600×2450 (Ш×Г×В). Перед раскроем — контрольный замер цеха после чистовой отделки стен, пола и потолка.
2. Корпус — ЛДСП 16 мм, задняя стенка ХДФ 4 мм в паз, цоколь 80 мм на регулируемых опорах; двери купе — МДФ, шпон ореха 10 мм, масло матовое в профиле: латунь; нахлёст 30 мм, ширина двери 840 мм, высота — проём минус 40 мм; цвет — по колерной карте.
3. Кромка: скрытые торцы 0,4 мм, видимые 2 мм (ПВХ/АБС).
4. Номинальные зазоры: дверь купе — боковина 3 мм, фасад ящика — стойка 2 мм; ящики внутри купе — с накладкой 30 мм на стойке со стороны нахлёста дверей.
5. Присадка по 32-й системе — выполняет цех.
6. Компенсатор 100 мм — короб из ЛДСП по фронту и торцам, подгоняется к потолку при монтаже (припуск 20 мм), крепится к корпусу и к потолку.
7. Подъём корпуса: диагональ боковины без цоколя $\sqrt{(2370^2 + 600^2)} = 2445$ мм < 2550 мм до потолка — корпус собирается лёжа, поднимается поворотом и ставится на цоколь.
8. Крепление к стене от опрокидывания — уголки 2 шт. к несущему основанию (монтажная схема шкафов).

## Условные обозначения

- дверь купе, стрелка — направление движения
- корпус и полки ЛДСП (вид на стену)
- задняя стенка ХДФ
- деталь в разрезе
- компенсатор — короб до потолка
- штанга для плечиков (на разрезе — плечики 450 мм)
- траектория угла корпуса при подъёме в проектное положение

**Допущения и предложения на листе**

Основа листа: размеры сняты со скана обмерного плана KV оформление (см): часть подписей не читается, помещения выровнены по читаемым размерам; контрольный обмер не выполнен (К-1); высота потолка 2650 мм принята по отметкам обмера (Н = 2,50…2,66 м, ригель 2,28 м) — уточнить при обмере (К-2); толщины стен 300 / 120 мм приняты, межквартирная стена и колонны — по скану, не замерены (К-1); разрешённая мощность 15 кВт принята по типовым ТУ; при объединении двух квартир — переоформление ТУ (К-4); подрайон климата не задан — принят не северный (жилые от 2,5 м) (К-8).

См. лист открытых вопросов (лист 6, записи К-1, К-2, К-4, К-8).

1000 мм · печать 1:1

| Изм. | Кол.уч | Лист | № док. | Подп. | Дата |
|---|---|---|---|---|---|
| Разраб. | | Кырлан А.С. | | | 04.11.26 |
| Пров. | | | | | |
| ГИП | | | | | |
| Н. контр. | | | | | |
| Утв. | | | | | |

**ГД-2026-009-АИ**

Квартира 103 м²

Общая площадь 100,72* м² · * размеры со скана, не замерены (реестр — л. 6, 7, К-1)

Дизайн-проект интерьера

| Стадия | Лист | Листов |
|---|---|---|
| РП | 68 | 120 |

**Шкаф-купе П1**

М 1:40

**Кырлан Александр Сергеевич**


выпуск 04.11.2026 № 35b47f1c2a · стр. 76 из 130

# Система хранения Пс1


Постирочная (пом. 7) · вид из помещения · размеры в мм, отметки в м

ПРЕДВАРИТЕЛЬНО · не для производства работ · открыто пунктов: 8 (реестр — л. 6, 7)


**Общий вид**

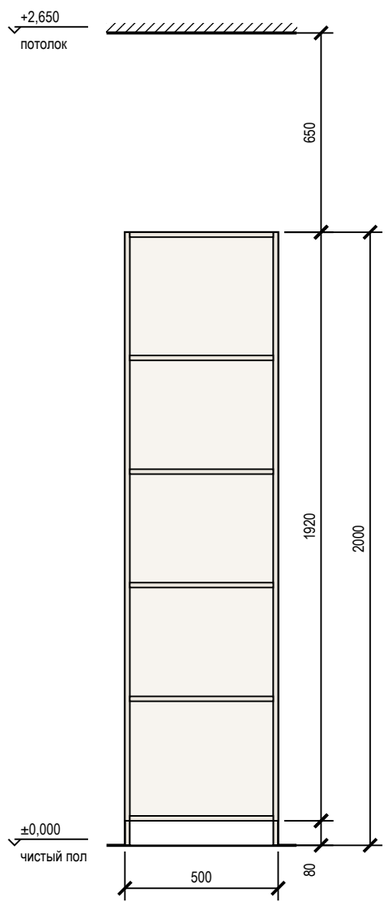


**Наполнение, размеры в свету**

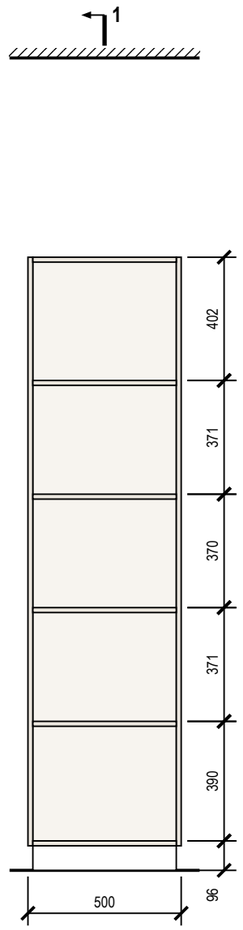


**Разрез 1-1**

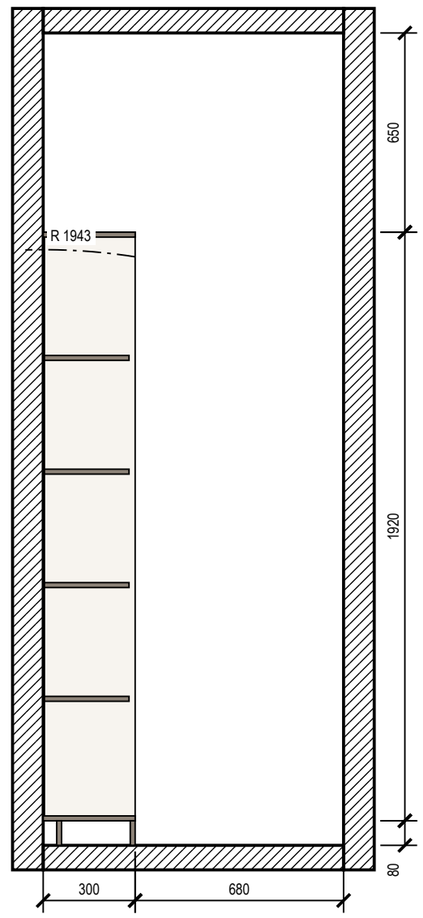


## Примечания

1. Размеры — в мм по чистовой отделке; изделие 500×300×2000 (Ш×Г×В). Перед раскроем — контрольный замер цеха после чистовой отделки стен, пола и потолка.
2. Корпус — ЛДСП 16 мм, задняя стенка ХДФ 4 мм в паз, цоколь 80 мм на регулируемых опорах; открытая система: без фасадов.
3. Кромка: скрытые торцы 0,4 мм, видимые 2 мм (ПВХ/АБС).
4. Присадка по 32-й системе — выполняет цех.
5. Зазор до потолка 650 мм.
6. Подъём корпуса: диагональ боковины без цоколя √(1920² + 300²) = 1943 мм < 2650 мм до потолка — корпус собирается лёжа, поднимается поворотом и ставится на цоколь.
7. Крепление к стене от опрокидывания — уголки 2 шт. к несущему основанию (монтажная схема шкафов).
8. Проход перед изделием 680 мм показан на разрезе 1-1.

## Условные обозначения

- корпус и полки ЛДСП (вид на стену)
- задняя стенка ХДФ
- деталь в разрезе
- штанга для плечиков (на разрезе — плечики 450 мм)
- траектория угла корпуса при подъёме в проектное положение

**Допущения и предложения на листе**

Основа листа: размеры сняты со скана обмерного плана KV оформление (см): часть подписей не читается, помещения выровнены по читаемым размерам; контрольный обмер не выполнен (К-1); высота потолка 2650 мм принята по отметкам обмера (Н = 2,50…2,66 м, ригель 2,28 м) — уточнить при обмере (К-2); толщины стен 300 / 120 мм приняты, межквартирная стена и колонны — по скану, не замерены (К-1); разрешённая мощность 15 кВт принята по типовым ТУ; при объединении двух квартир — переоформление ТУ (К-4); подрайон климата не задан — принят не северный (жилые от 2,5 м) (К-8).
См. лист открытых вопросов (лист 6, записи К-1, К-2, К-4, К-8).

1000 мм · печать 1:1

| Изм. | Кол.уч | Лист | № док. | Подп. | Дата |
|---|---|---|---|---|---|
| Разраб. | | Кырлан А.С. | | | 04.11.26 |
| Пров. | | | | | |
| ГИП | | | | | |
| | | | | | |
| Н. контр. | | | | | |
| Утв. | | | | | |

**ГД-2026-009-АИ**

Квартира 103 м²

Общая площадь 100,72* м² · * размеры со скана, не замерены (реестр — л. 6, 7, К-1)

Дизайн-проект интерьера

| Стадия | Лист | Листов |
|---|---|---|
| РП | 69 | 120 |

**Система хранения Пс1**

М 1:20

**Кырлан Александр Сергеевич**


выпуск 04.11.2026 № 35b47f1c2a · стр. 77 из 130

# Шкаф распашной С2


Спальня 2 (пом. 8) · вид из помещения · размеры в мм, отметки в м

**ПРЕДВАРИТЕЛЬНО · не для производства работ · открыто пунктов: 8 (реестр — л. 6, 7)**


**Вид с фасадами**

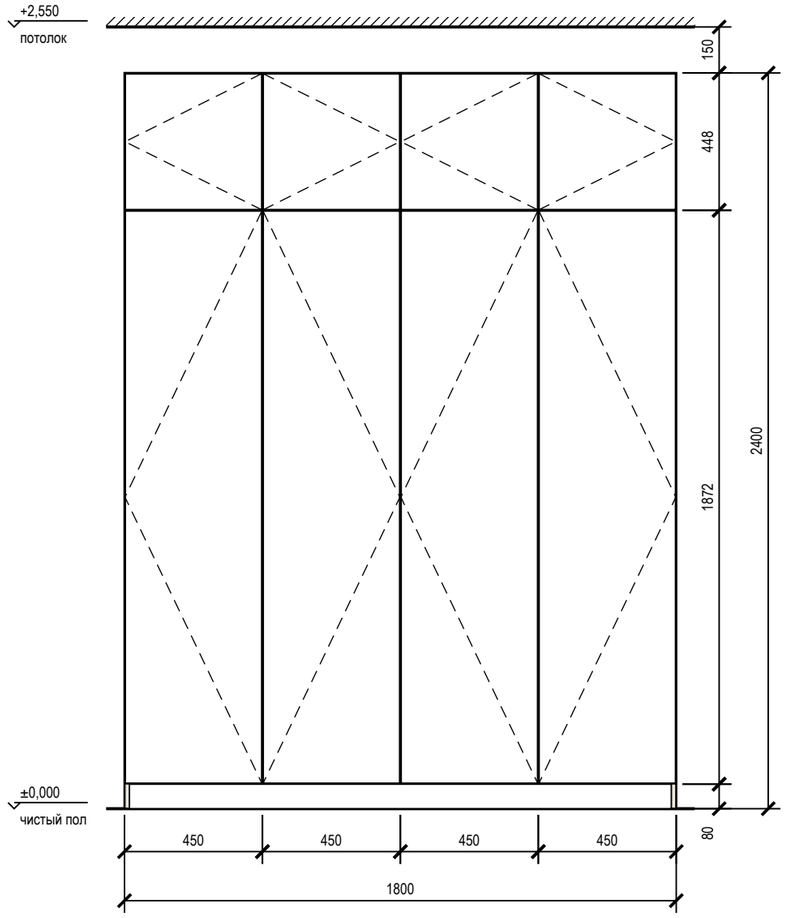



**Вид без фасадов**

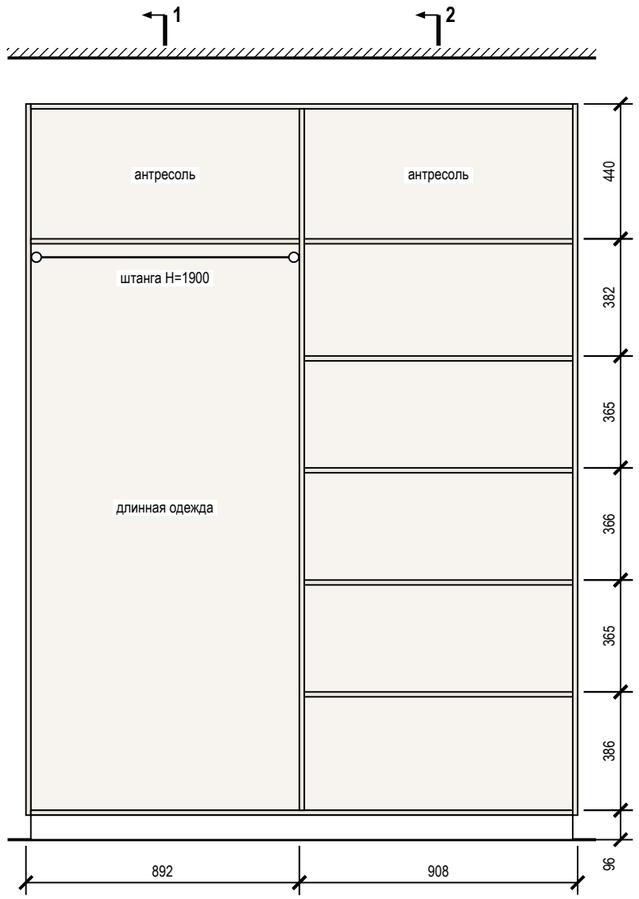


**Разрез 1-1**

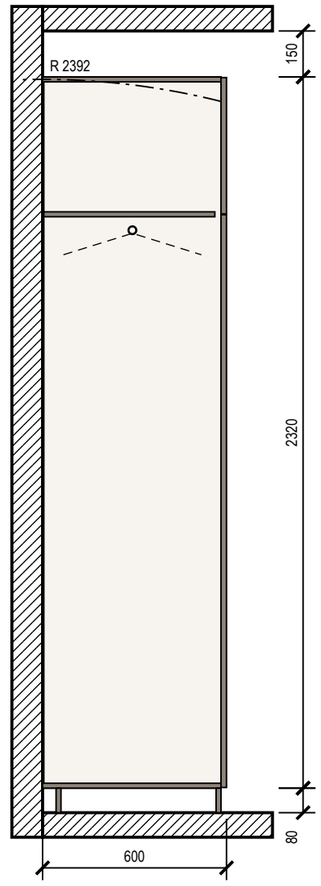


**Разрез 2-2**

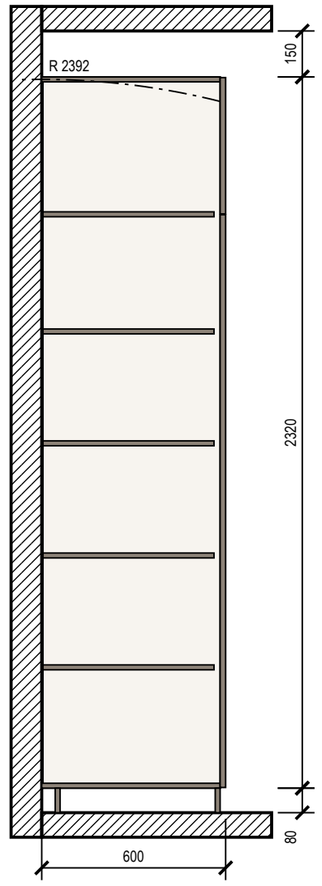


## Примечания

1. Размеры — в мм по чистовой отделке; изделие 1800×600×2400 (Ш×Г×В). Перед раскроем — контрольный замер цеха после чистовой отделки стен, пола и потолка.
2. Корпус — ЛДСП 16 мм, задняя стенка ХДФ 4 мм в паз, цоколь 80 мм на регулируемых опорах; фасады накладные — МДФ, шпон ореха 18 мм, масло матовое; цвет — по колерной карте; петли с доводчиком: фасад 1869 мм — 4 петли, фасад 445 мм — 2 петли.
3. Кромка: скрытые торцы 0,4 мм, видимые 2 мм (ПВХ/АБС).
4. Номинальные зазоры: между фасадами 3 мм, фасад — стена и фасад — потолок не менее 3 мм, фасад ящика — стойка 2 мм.
5. Присадка по 32-й системе — выполняет цех.
6. Зазор до потолка 150 мм — закрыть планкой в цвет корпуса при монтаже.
7. Подъём корпуса: диагональ боковины без цоколя √(2320² + 582²) = 2392 мм < 2550 мм до потолка — корпус собирается лёжа, поднимается поворотом и ставится на цоколь.
8. Крепление к стене от опрокидывания — уголки 2 шт. к несущему основанию (монтажная схема шкафов).

## Условные обозначения

- фасад распашной: линии сходятся к стороне петель
- корпус и полки ЛДСП (вид на стену)
- задняя стенка ХДФ
- деталь в разрезе
- штанга для плечиков (на разрезе — плечики 450 мм)
- траектория угла корпуса при подъёме в проектное положение

**Допущения и предложения на листе**

Основа листа: размеры сняты со скана обмерного плана KV оформление (см): часть подписей не читается, помещения выровнены по читаемым размерам; контрольный обмер не выполнен (К-1); высота потолка 2650 мм принята по отметкам обмера (Н = 2,50…2,66 м, ригель 2,28 м) — уточнить при обмере (К-2); толщины стен 300 / 120 мм приняты, межквартирная стена и колонны — по скану, не замерены (К-1); разрешённая мощность 15 кВт принята по типовым ТУ; при объединении двух квартир — переоформление ТУ (К-4); подрайон климата не задан — принят не северный (жилые от 2,5 м) (К-8).

См. лист открытых вопросов (лист 6, записи К-1, К-2, К-4, К-8).

1000 мм · печать 1:1

| Изм. | Кол.уч | Лист | № док. | Подп. | Дата |
|---|---|---|---|---|---|
| Разраб. | | Кырлан А.С. | | | 04.11.26 |
| Пров. | | | | | |
| ГИП | | | | | |
| Н. контр. | | | | | |
| Утв. | | | | | |

**ГД-2026-009-АИ**

Квартира 103 м²

Общая площадь 100,72* м² · * размеры со скана, не замерены (реестр — л. 6, 7, К-1)

Дизайн-проект интерьера

| Стадия | Лист | Листов |
|---|---|---|
| РП | 70 | 120 |

**Шкаф распашной С2**

М 1:20

**Кырлан Александр Сергеевич**


выпуск 04.11.2026 № 35b47f1c2a · стр. 78 из 130

# Шкаф распашной М4


Спальня мастер (пом. 10) · вид из помещения · размеры в мм, отметки в м

**ПРЕДВАРИТЕЛЬНО · не для производства работ · открыто пунктов: 8 (реестр — л. 6, 7)**


## Вид с фасадами

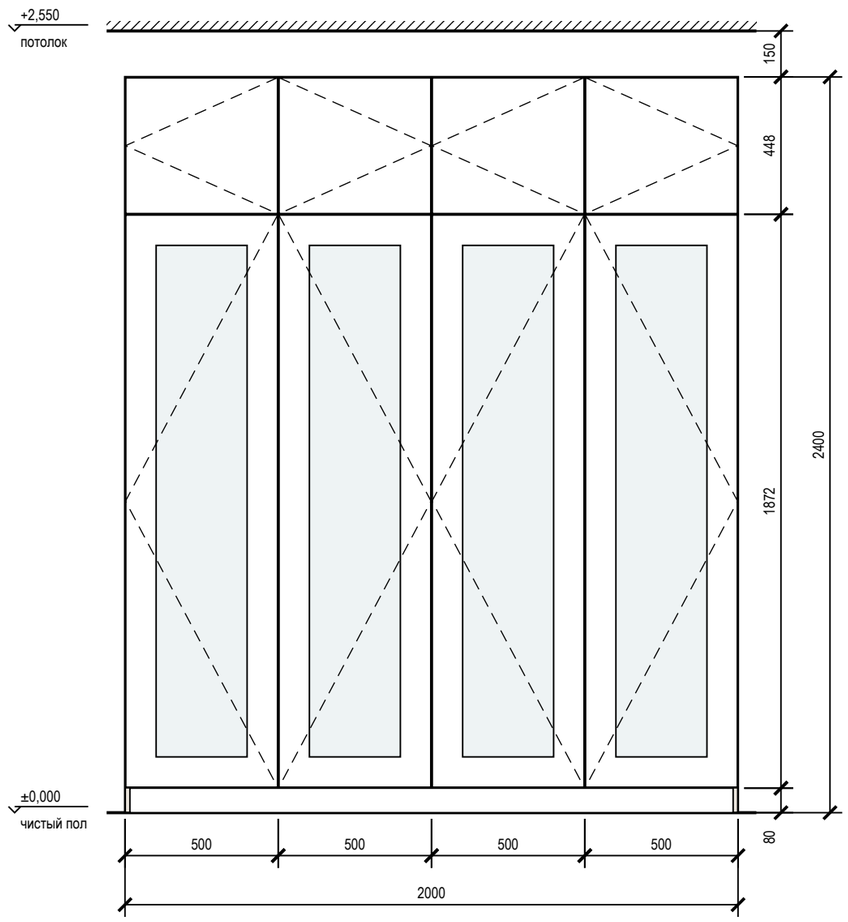



## Вид без фасадов

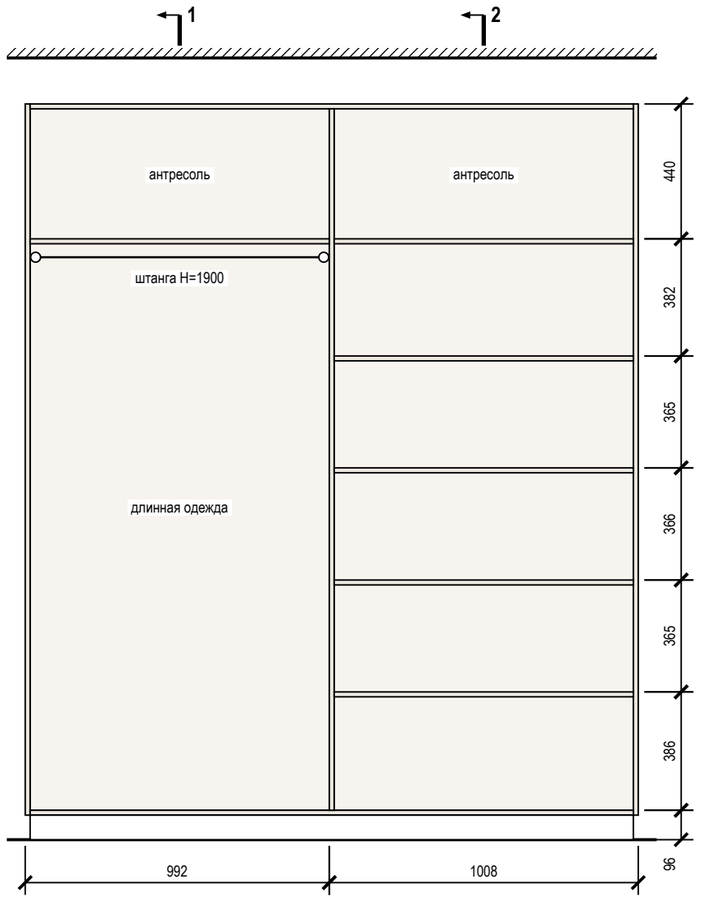


## Разрез 1-1

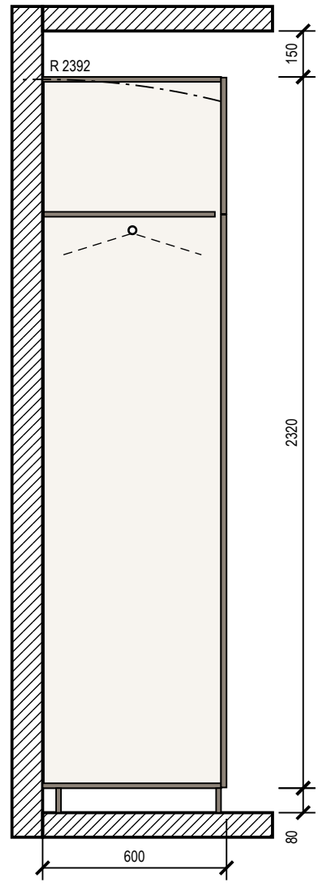


## Разрез 2-2

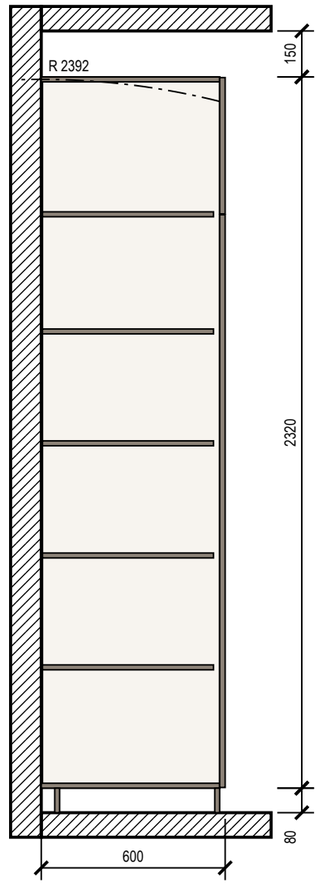


## Примечания

1. Размеры — в мм по чистовой отделке; изделие 2000×600×2400 (Ш×Г×В). Перед раскроем — контрольный замер цеха после чистовой отделки стен, пола и потолка.
2. Корпус — ЛДСП 16 мм, задняя стенка ХДФ 4 мм в паз, цоколь 80 мм на регулируемых опорах; фасады накладные — МДФ, шпон ореха 18 мм, масло матовое; вставка — латунь; цвет — по колерной карте; петли с доводчиком: фасад 1869 мм — 4 петли, фасад 445 мм — 2 петли.
3. Кромка: скрытые торцы 0,4 мм, видимые 2 мм (ПВХ/АБС).
4. Номинальные зазоры: между фасадами 3 мм, фасад — стена и фасад — потолок не менее 3 мм, фасад ящика — стойка 2 мм.
5. Присадка по 32-й системе — выполняет цех.
6. Зазор до потолка 150 мм — закрыть планкой в цвет корпуса при монтаже.
7. Подъём корпуса: диагональ боковины без цоколя √(2320² + 582²) = 2392 мм < 2550 мм до потолка — корпус собирается лёжа, поднимается поворотом и ставится на цоколь.
8. Крепление к стене от опрокидывания — уголки 2 шт. к несущему основанию (монтажная схема шкафов).

## Условные обозначения

- фасад распашной: линии сходятся к стороне петель
- корпус и полки ЛДСП (вид на стену)
- задняя стенка ХДФ
- деталь в разрезе
- штанга для плечиков (на разрезе — плечики 450 мм)
- траектория угла корпуса при подъёме в проектное положение

**Допущения и предложения на листе**

Основа листа: размеры сняты со скана обмерного плана KV оформление (см): часть подписей не читается, помещения выровнены по читаемым размерам; контрольный обмер не выполнен (К-1); высота потолка 2650 мм принята по отметкам обмера (Н = 2,50…2,66 м, ригель 2,28 м) — уточнить при обмере (К-2); толщины стен 300 / 120 мм приняты, межквартирная стена и колонны — по скану, не замерены (К-1); разрешённая мощность 15 кВт принята по типовым ТУ; при объединении двух квартир — переоформление ТУ (К-4); подрайон климата не задан — принят не северный (жилые от 2,5 м) (К-8).
См. лист открытых вопросов (лист 6, записи К-1, К-2, К-4, К-8).

1000 мм · печать 1:1

| Изм. | Кол.уч | Лист | № док. | Подп. | Дата |
|---|---|---|---|---|---|
| Разраб. | | Кырлан А.С. | | | 04.11.26 |
| Пров. | | | | | |
| ГИП | | | | | |
| Н. контр. | | | | | |
| Утв. | | | | | |

**ГД-2026-009-АИ**

Квартира 103 м²

Общая площадь 100,72* м² · * размеры со скана, не замерены (реестр — л. 6, 7, К-1)

Дизайн-проект интерьера

| Стадия | Лист | Листов |
|---|---|---|
| РП | 71 | 120 |

**Шкаф распашной М4**

М 1:20

**Кырлан Александр Сергеевич**


выпуск 04.11.2026 № 35b47f1c2a · стр. 79 из 130

# Кухня (пом. 5). Развёртка гарнитура


Кухня (пом. 5) · стена Б · вид из помещения · размеры в мм, отметки в м

ПРЕДВАРИТЕЛЬНО · не для производства работ · открыто пунктов: 8 (реестр — л. 6, 7)


**Вид с фасадами**

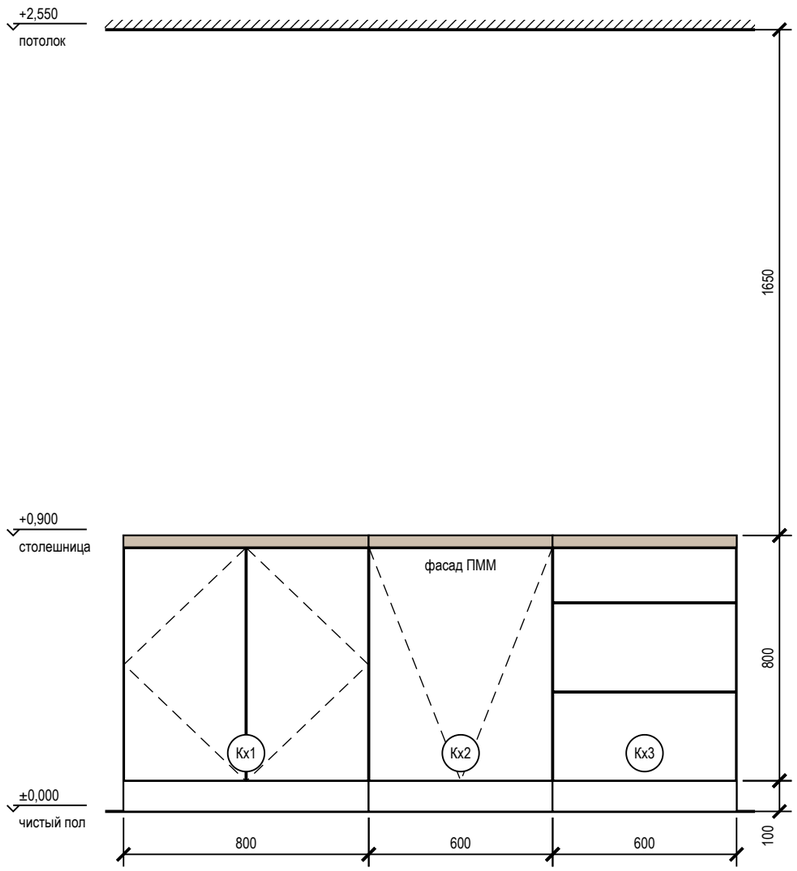


**Вид без фасадов (наполнение, выводы)**

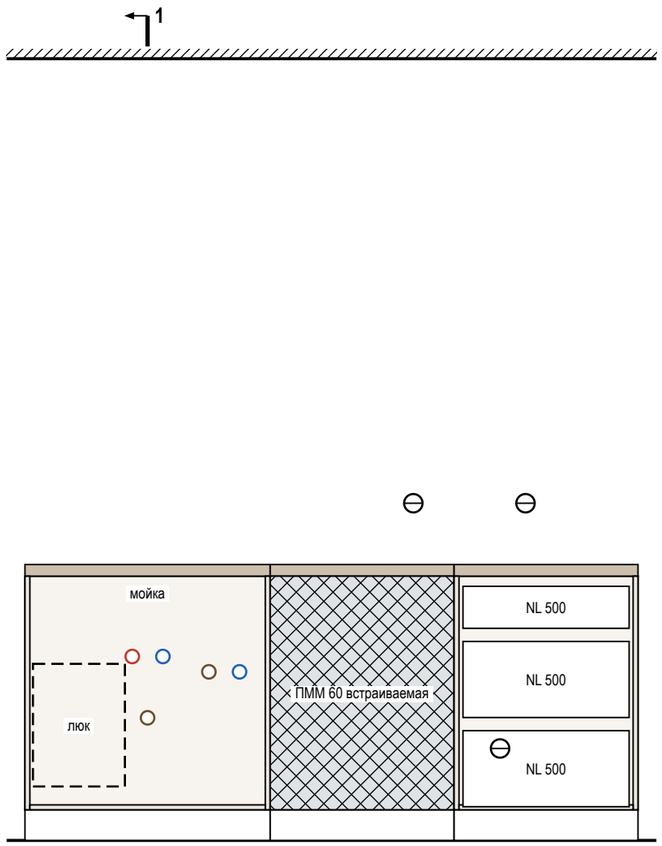


**Разрез 1-1**

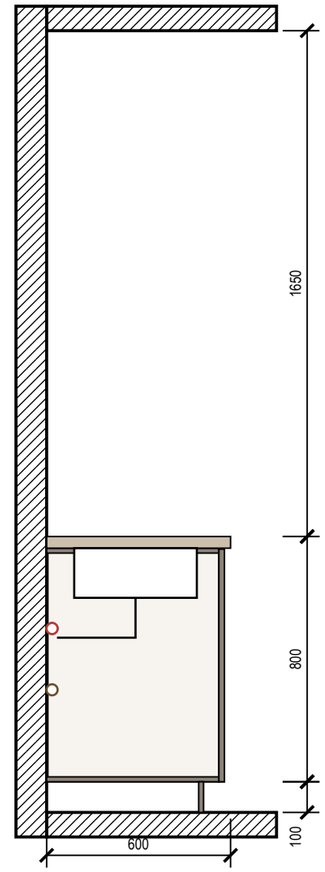


## Условные обозначения

- фасад распашной: линии сходятся к стороне петель
- фасад ящика, карго
- встраиваемая техника
- столешница
- доборная планка
- деталь в разрезе
- К1 — марка изделия или модуля (на схеме расположения под ней — лист изделия)
- розетка на стене
- вывод кабеля к технике
- В1 — вывод воды В1 / Т3, канализации К1

## Примечания

1. Размеры — в мм по чистовой отделке, вид из помещения; марки — как на плане расстановки. Перед раскроем — контрольный замер цеха после фартука и пола.
2. Корпуса — ЛДСП 16 мм, задняя стенка ХДФ 4 мм; фасады — МДФ, шпон ореха 18 мм, цвет по колерной карте; столешница 38 мм, свес 20 мм; цоколь 100 мм.
3. Кромка: скрытые торцы 0,4 мм, видимые 2 мм. Номинальные зазоры: между фасадами 3 мм, фасад — столешница 3 мм, фасад — стена не менее 3 мм.
4. Ящики полного выдвижения и петли — с доводчиком; присадка по 32-й системе — выполняет цех.
5. Ниши техники — по монтажным схемам выбранных моделей: решётка в цоколе и канал за пеналом холодильника, зазор за духовым шкафом, фасад ПММ на двери машины.
6. Кх1: сервисный люк к стоякам Ст К1-2 (кухня), Ст В1-2, Ст Т3-2 — съёмная панель 300×400 мм в задней стенке на саморезах (по виду без фасадов, штриховой контур «люк»), доступ через фасад модуля; короб стояков за модулем — с ревизией напротив люка (лист ВК).

**Допущения и предложения на листе**

Основа листа: размеры сняты со скана обмерного плана KV оформление (см): часть подписей не читается, помещения выровнены по читаемым размерам; контрольный обмер не выполнен (К-1); высота потолка 2650 мм принята по отметкам обмера (Н = 2,50…2,66 м, ригель 2,28 м) — уточнить при обмере (К-2); толщины стен 300 / 120 мм приняты, межквартирная стена и колонны — по скану, не замерены (К-1); разрешённая мощность 15 кВт принята по типовым ТУ; при объединении двух квартир — переоформление ТУ (К-4); подрайон климата не задан — принят не северный (жилые от 2,5 м) (К-8).
См. лист открытых вопросов (лист 6, записи К-1, К-2, К-4, К-8).

1000 мм · печать 1:1

| Изм. | Кол.уч | Лист | № док. | Подп. | Дата |
|---|---|---|---|---|---|
| Разраб. | | Кырлан А.С. | | | 04.11.26 |
| Пров. | | | | | |
| ГИП | | | | | |
| Н. контр. | | | | | |
| Утв. | | | | | |

**ГД-2026-009-АИ**

Квартира 103 м²

Общая площадь 100,72* м² · * размеры со скана, не замерены (реестр — л. 6, 7, К-1)

| Дизайн-проект интерьера | Стадия | Лист | Листов |
|---|---|---|---|
| | РП | 72 | 120 |

**Кухня (пом. 5). Развёртка гарнитура**

М 1:20

**Кырлан Александр Сергеевич**


выпуск 04.11.2026 № 35b47f1c2a · стр. 80 из 130

# Кухня (пом. 5). Монтажная схема


Кухня (пом. 5) · стена Б · размеры в мм от чистых поверхностей, высоты — от чистого пола

**ПРЕДВАРИТЕЛЬНО · не для производства работ · открыто пунктов: 8 (реестр — л. 6, 7)**

## Привязка выводов и крепление модулей

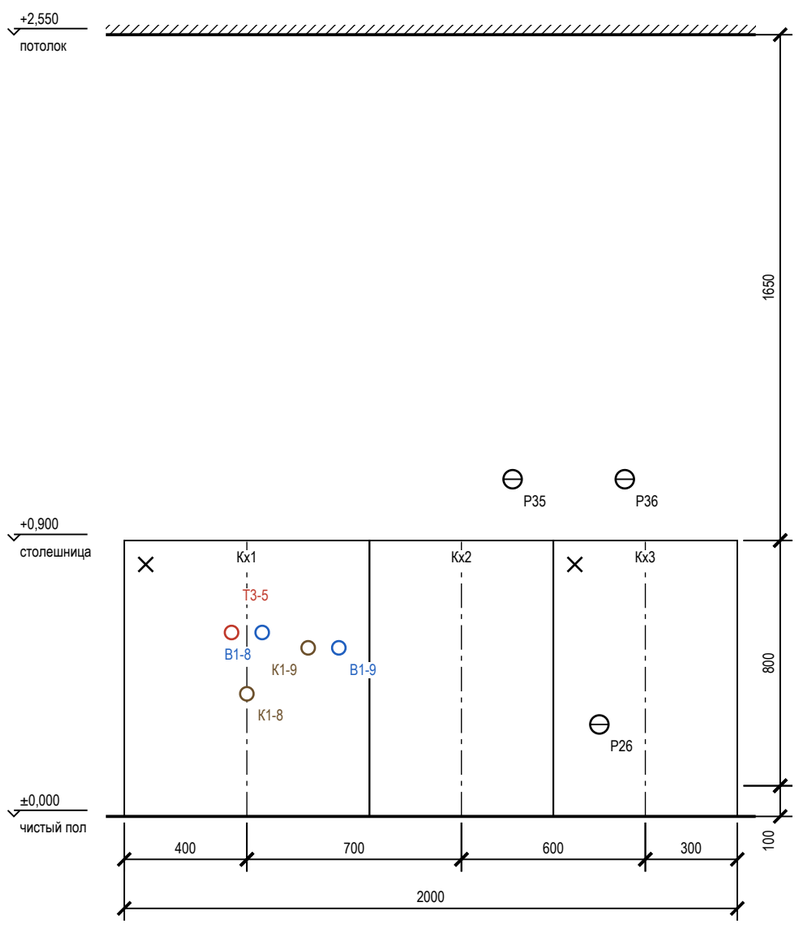


## План столешницы

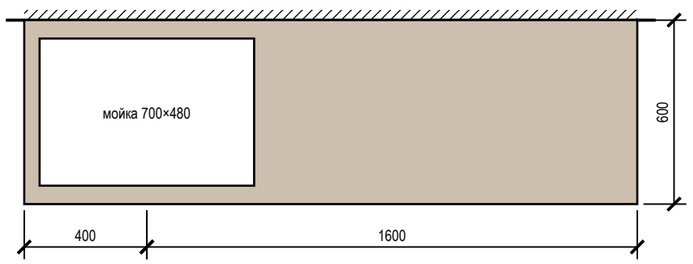


## Привязка выводов к осям модулей

| Код | Назначение | Модуль | От оси, мм | H, мм | Размещение |
|---|---|---|---|---|---|
| Т3-5 | Т3 — межос. 100 | Кх1 | −50 | 600 | в модуле мойки |
| К1-8 | К1 Ø50 — мойка | Кх1 | 0 | 400 | в модуле мойки |
| В1-8 | В1 — межос. 100 | Кх1 | +50 | 600 | в модуле мойки |
| К1-9 | К1 Ø40 — слив ПММ в шкафу мойки | Кх1 | +200 | 550 | в модуле мойки |
| В1-9 | В1 — кран ПММ в шкафу мойки | Кх1 | +300 | 550 | в модуле мойки |
| Р35 | розетка ×2 — фартук | Кх2 | +167 | 1100 | над столешницей (фартук) |
| Р26 | розетка — посудомоечная машина — в соседнем модуле, за ящиком | Кх3 | −150 | 300 | в соседнем модуле, за ящиком |
| Р36 | розетка ×2 — фартук | Кх3 | −67 | 1100 | над столешницей (фартук) |

## Зазоры под отделку

| Поверхность | Отделка | Зазор, мм | Учесть |
|---|---|---|---|
| фартук | керамогранит | 10 | от чернового основания до корпуса навесных и столешницы |
| стены | окраска | 5 | под штукатурку и шпаклёвку за пеналом |
| пол | инженерная доска | | цоколь — после укладки пола, опоры ±20 мм |

## Условные обозначения

- нижний модуль, пенал (контур)
- ось модуля (от неё — привязка вывода)
- анкер / уголок крепления к стене
- розетка на стене
- вывод кабеля к технике
- В1 — вывод воды В1 / Т3, канализации К1

## Примечания

1. Выводы — по проекту электрики и ВК; привязка по горизонтали — от оси модуля (плюс — вправо по виду), по высоте — от чистого пола до оси вывода.
2. Пенал — уголки к стене 2 шт. сверху; нижние модули — стяжками между собой и уголком к стене; ряд выставить по уровню опорами цоколя.
3. Розетки над столешницей — не ниже 150 мм над ней и не за корпусом техники; розетка за ПММ, духовым шкафом и холодильником — только в соседнем модуле или в зоне цоколя с доступом.
4. Столешница — вырезы по шаблонам выбранных моделей мойки и варочной панели; торцы у стены — герметик, пристеночный плинтус.

**Допущения и предложения на листе**

Основа листа: размеры сняты со скана обмерного плана KV оформление (см): часть подписей не читается, помещения выровнены по читаемым размерам; контрольный обмер не выполнен (К-1); высота потолка 2650 мм принята по отметкам обмера (H = 2,50…2,66 м, ригель 2,28 м) — уточнить при обмере (К-2); толщины стен 300 / 120 мм приняты, межквартирная стена и колонны — по скану, не замерены (К-1); разрешённая мощность 15 кВт принята по типовым ТУ; при объединении двух квартир — переоформление ТУ (К-4); подрайон климата не задан — принят не северный (жилые от 2,5 м) (К-8).

См. лист открытых вопросов (лист 6, записи К-1, К-2, К-4, К-8).

1000 мм · печать 1:1

| Изм. | Кол.уч | Лист | № док. | Подп. | Дата |
|---|---|---|---|---|---|
| Разраб. | | Кырлан А.С. | | | 04.11.26 |
| Пров. | | | | | |
| ГИП | | | | | |
| | | | | | |
| Н. контр. | | | | | |
| Утв. | | | | | |

**ГД-2026-009-АИ**

Квартира 103 м²

Общая площадь 100,72* м² · * размеры со скана, не замерены (реестр — л. 6, 7, К-1)

Дизайн-проект интерьера

| Стадия | Лист | Листов |
|---|---|---|
| РП | 73 | 120 |

**Кухня (пом. 5). Монтажная схема**

М 1:20

**Кырлан Александр Сергеевич**


выпуск 04.11.2026 № 35b47f1c2a · стр. 81 из 130

# Кухня (пом. 5). Развёртка гарнитура


Кухня (пом. 5) · стена В · вид из помещения · размеры в мм, отметки в м

ПРЕДВАРИТЕЛЬНО · не для производства работ · открыто пунктов: 8 (реестр — л. 6, 7)


**Вид с фасадами**

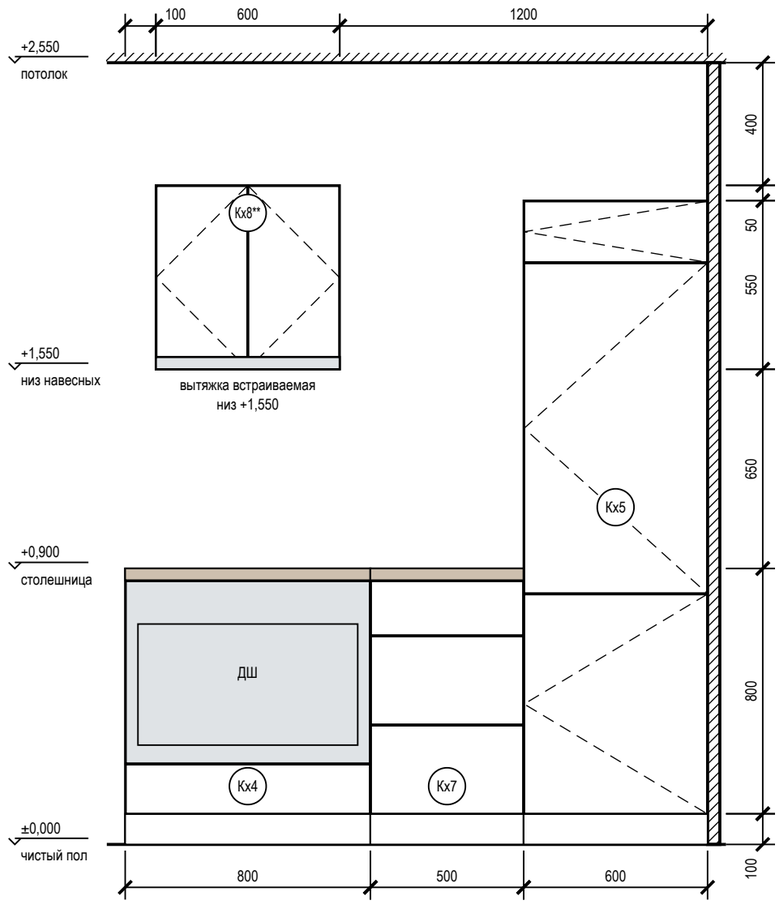



**Вид без фасадов (наполнение, выводы)**

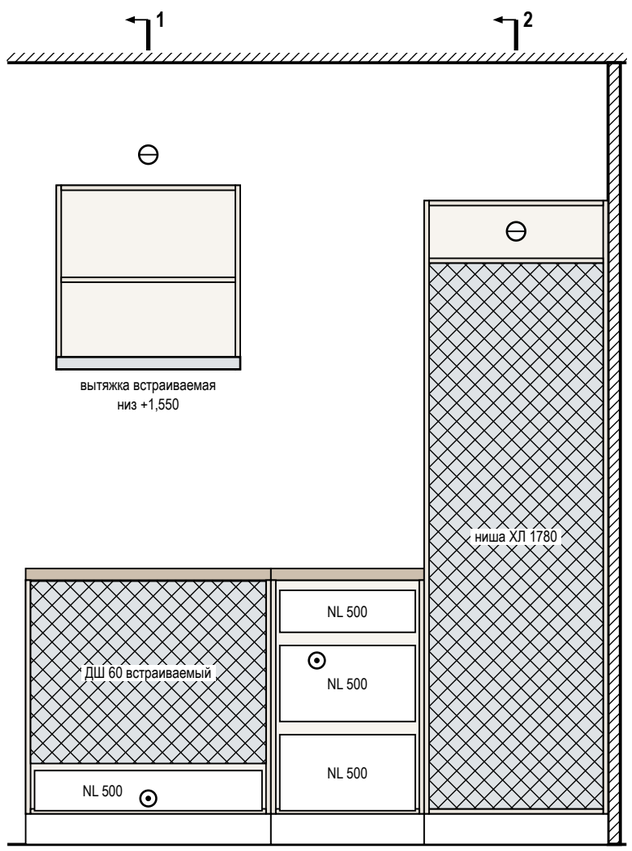


**Разрез 1-1**

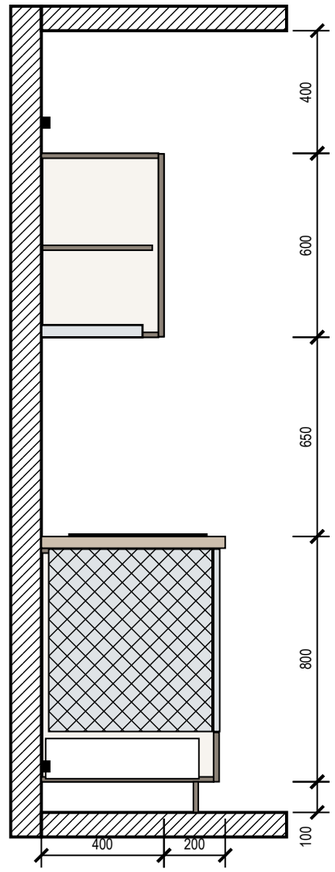


**Разрез 2-2**

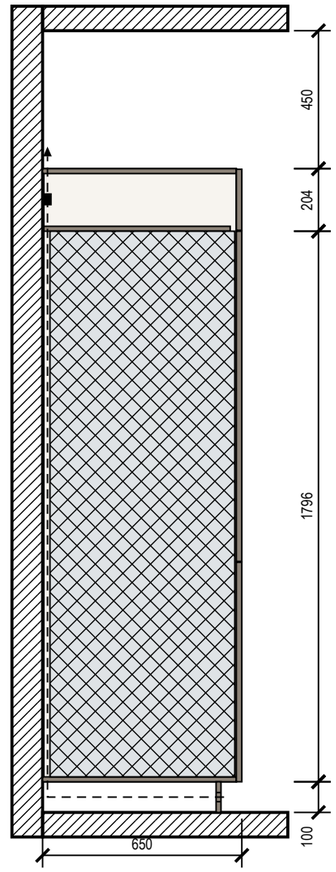


## Условные обозначения

- фасад распашной: линии сходятся к стороне петель
- фасад ящика, карго
- встраиваемая техника
- столешница
- доборная планка
- деталь в разрезе
- К1 — марка изделия или модуля (на схеме расположения под ней — лист изделия)
- розетка на стене
- вывод кабеля к технике
- В1 — вывод воды В1 / Т3, канализации К1

1000 мм · печать 1:1

## Примечания

1. Размеры — в мм по чистовой отделке, вид из помещения; марки — как на плане расстановки. Перед раскроем — контрольный замер цеха после фартука и пола.
2. Корпуса — ЛДСП 16 мм, задняя стенка ХДФ 4 мм; фасады — МДФ, эмаль матовая 18 мм, цвет по колерной карте; столешница 38 мм, свес 20 мм; цоколь 100 мм.
3. Кромка: скрытые торцы 0,4 мм, видимые 2 мм. Номинальные зазоры: между фасадами 3 мм, фасад — столешница 3 мм, фасад — стена не менее 3 мм.
4. Ящики полного выдвижения и петли — с доводчиком; присадка по 32-й системе — выполняет цех.
5. Вытяжка встраивается в дно навесного модуля Кх8** над варочной: её низ на 1550 мм от пола, 650 мм над панелью (не меньше 650 мм).
6. Ниши техники (холодильник — ориентир 1780 мм) — по монтажным схемам выбранных моделей: решётка в цоколе и канал за пеналом холодильника, зазор за духовым шкафом, фасад ПММ на двери машины.

**Допущения и предложения на листе**

Основа листа: размеры сняты со скана обмерного плана KV оформление (см): часть подписей не читается, помещения выровнены по читаемым размерам; контрольный обмер не выполнен (К-1); высота потолка 2650 мм принята по отметкам обмера (Н = 2,50…2,66 м, ригель 2,28 м) — уточнить при обмере (К-2); толщины стен 300 / 120 мм приняты, межквартирная стена и колонны — по скану, не замерены (К-1); разрешённая мощность 15 кВт принята по типовым ТУ; при объединении двух квартир — переоформление ТУ (К-4); подрайон климата не задан — принят не северный (жилые от 2,5 м) (К-8).
Знак «**» — предложение проектировщика, заказчиком не утверждено (согласовать с заказчиком): Кх8 — над индукционной панелью Кх4 нужна вытяжка: в составе кухни её не было, розетка вытяжки образца висела без потребителя.
См. лист открытых вопросов (лист 6, записи К-1, К-2, К-4, К-8).

| Изм. | Кол.уч | Лист | № док. | Подп. | Дата |
|---|---|---|---|---|---|
| Разраб. | | Кырлан А.С. | | | 04.11.26 |
| Пров. | | | | | |
| ГИП | | | | | |
| | | | | | |
| Н. контр. | | | | | |
| Утв. | | | | | |

**ГД-2026-009-АИ**

Квартира 103 м²

Общая площадь 100,72* м² · * размеры со скана, не замерены (реестр — л. 6, 7, К-1)

| Дизайн-проект интерьера | Стадия | Лист | Листов |
|---|---|---|---|
| | РП | 74 | 120 |

**Кухня (пом. 5). Развёртка гарнитура**

М 1:20

**Кырлан Александр Сергеевич**


выпуск 04.11.2026 № 35b47f1c2a · стр. 82 из 130

# Кухня (пом. 5). Монтажная схема


Кухня (пом. 5) · стена В · размеры в мм от чистых поверхностей, высоты — от чистого пола



## Привязка выводов и крепление модулей

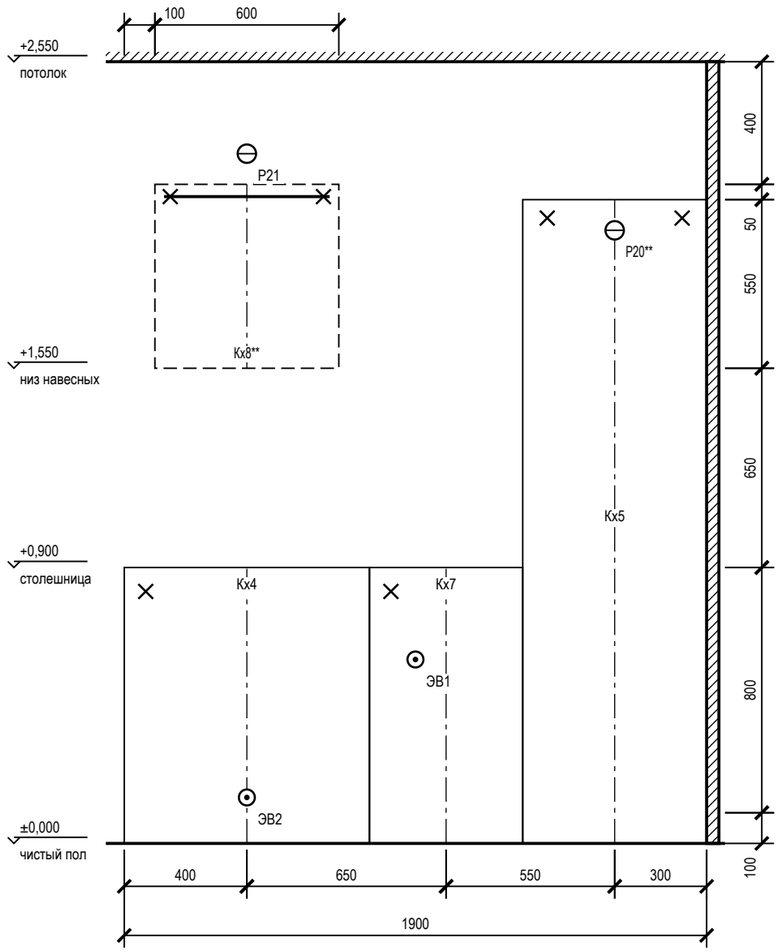


## План столешницы

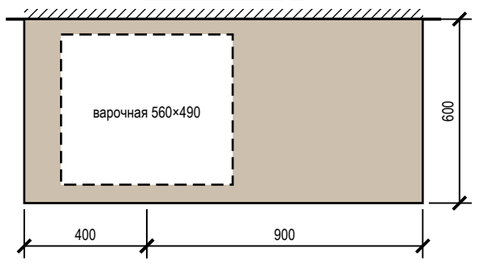


## Привязка выводов к осям модулей

| Код | Назначение | Модуль | От оси, мм | Н, мм | Размещение |
|---|---|---|---|---|---|
| ЭВ2 | вывод кабеля — духовой шкаф — в цоколе | Кх4 | 0 | 150 | под духовым шкафом, доступ через ящик |
| P21 | розетка — вытяжка — над корпусом | Кх8** | 0 | 2250 | в навесном модуле |
| ЭВ1 | вывод кабеля — варочная панель — в соседнем модуле, за ящиком | Кх7 | −100 | 600 | в соседнем модуле, за ящиком |
| P20** | розетка — холодильник — над нишей, съёмная панель | Кх5 | 0 | 2000 | над нишей холодильника, съёмная панель |

## Зазоры под отделку

| Поверхность | Отделка | Зазор, мм | Учесть |
|---|---|---|---|
| фартук | керамогранит | 10 | от чернового основания до корпуса навесных и столешницы |
| стены | окраска | 5 | под штукатурку и шпаклёвку за пеналом |
| пол | инженерная доска | | цоколь — после укладки пола, опоры ±20 мм |

## Условные обозначения

- нижний модуль, пенал (контур)
- невидимый контур: навесной модуль, корпус под столешницей
- ось модуля (от неё — привязка вывода)
- анкер / уголок крепления к стене
- розетка на стене
- вывод кабеля к технике
- B1 — вывод воды В1 / Т3, канализации К1

**Допущения и предложения на листе**

Основа листа: размеры сняты со скана обмерного плана KV оформление (см): часть подписей не читается, помещения выровнены по читаемым размерам; контрольный обмер не выполнен (К-1); высота потолка 2650 мм принята по отметкам обмера (Н = 2,50…2,66 м, ригель 2,28 м) — уточнить при обмере (К-2); толщины стен 300 / 120 мм приняты, межквартирная стена и колонны — по скану, не замерены (К-1); разрешённая мощность 15 кВт принята по типовым ТУ; при объединении двух квартир — переоформление ТУ (К-4); подрайон климата не задан — принят не северный (жилые от 2,5 м) (К-8).

Знак «**» — предложение проектировщика, заказчиком не утверждено (согласовать с заказчиком): Кх8 — над индукционной панелью Кх4 нужна вытяжка: в составе кухни её не было, розетка вытяжки образца висела без потребителя; Р20 — высота 2000 мм выше нормы 1 м (ПУЭ 6.6.30) по назначению: розетка встроенного прибора — в колонне Кх5 над нишей, в антресоли за съёмной панелью.

См. лист открытых вопросов (лист 6, записи К-1, К-2, К-4, К-8).

## Примечания

1. Выводы — по проекту электрики и ВК; привязка по горизонтали — от оси модуля (плюс — вправо по виду), по высоте — от чистого пола до оси вывода.
2. Пенал — уголки к стене 2 шт. сверху; нижние модули — стяжками между собой и уголком к стене; ряд выставить по уровню опорами цоколя.
3. Розетки над столешницей — не ниже 150 мм над ней и не за корпусом техники; розетка за ПММ, духовым шкафом и холодильником — только в соседнем модуле или в зоне цоколя с доступом.
4. Столешница — вырезы по шаблонам выбранных моделей мойки и варочной панели; торцы у стены — герметик, пристеночный плинтус.

1000 мм · печать 1:1

| Изм. | Кол.уч | Лист | № док. | Подп. | Дата |
|---|---|---|---|---|---|
| Разраб. | | Кырлан А.С. | | | 04.11.26 |
| Пров. | | | | | |
| ГИП | | | | | |
| Н. контр. | | | | | |
| Утв. | | | | | |

**ГД-2026-009-АИ**

Квартира 103 м²

Общая площадь 100,72* м² · * размеры со скана, не замерены (реестр — л. 6, 7, К-1)

Дизайн-проект интерьера

| Стадия | Лист | Листов |
|---|---|---|
| РП | 75 | 120 |

**Кухня (пом. 5). Монтажная схема**

М 1:20


**Кырлан Александр Сергеевич**

выпуск 04.11.2026 № 35b47f1c2a · стр. 83 из 130


# Шкафы. Монтажная схема

крепление к стене, установочные размеры, зазоры под отделку · размеры в мм


**Система хранения Кл1 (пом. 2)**

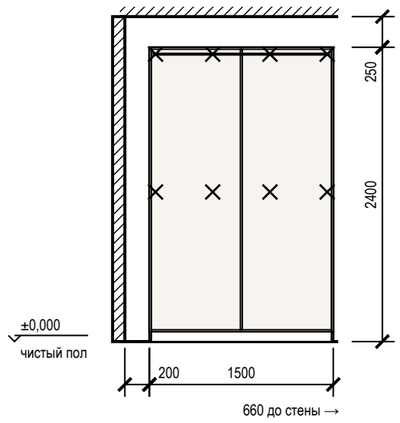



**Шкаф-купе П1 (пом. 4)**

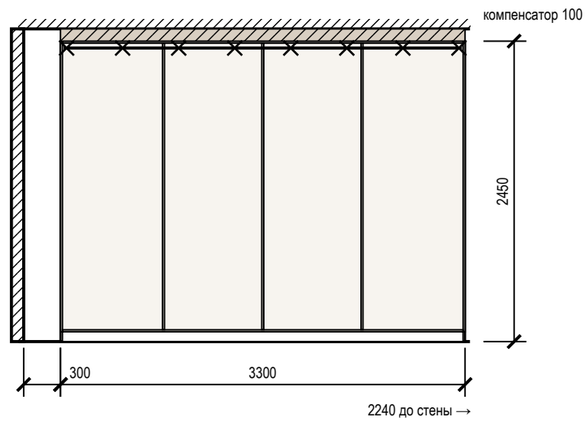



**Система хранения Пс1 пом. 7**

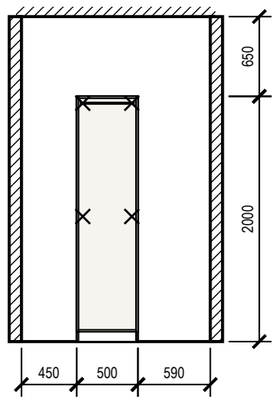


**Шкаф распашной С2 (пом. 8)**

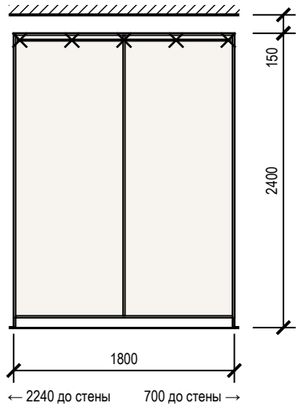


**Шкаф распашной М4 (пом. 10)**

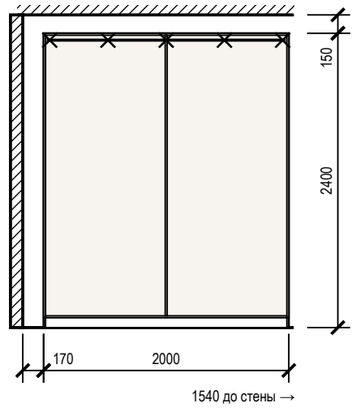


## Крепление и зазоры под отделку

| Марка | Помещение, стена | Основание | Отделка стены | Зазор, мм | Крепёж по планке | От опрокидывания |
|---|---|---|---|---|---|---|
| Кл1 | Кладовая (2), стена Б | по основанию — см. таблицу крепежа | окраска | 5 | анкер 8 шт. (2 ряда) | уголки 2 шт. |
| П1 | Прихожая-холл (4), стена А | по основанию — см. таблицу крепежа | окраска | 5 | анкер 8 шт., шаг 457 | уголки 2 шт. |
| Пс1 | Постирочная (7), стена Б | по основанию — см. таблицу крепежа | окраска | 5 | анкер 4 шт. (2 ряда) | уголки 2 шт. |
| С2 | Спальня 2 (8), стена А | по основанию — см. таблицу крепежа | окраска | 5 | анкер 5 шт., шаг 425 | уголки 2 шт. |
| М4 | Спальня мастер (10), стена Г | по основанию — см. таблицу крепежа | окраска | 5 | анкер 5 шт., шаг 475 | уголки 2 шт. |

## Крепёж по основанию стены

| Основание стены | Крепёж |
|---|---|
| бетон, ж/б | анкер-шуруп 7,5×72 или дюбель 8×60 с шурупом 5×70 |
| кирпич полнотелый | дюбель 8×80 с шурупом 5×90 |
| газобетон, пазогребень | дюбель для газобетона 10×100 или химический анкер |
| гипсокартон | закладная до обшивки (брус 40×80 или фанера 18 мм), саморез в закладную |

## Условные обозначения

- анкер / уголок крепления к стене
- корпус и полки ЛДСП (вид на стену)
- компенсатор — короб до потолка

## Примечания

1. Установочные размеры — от чистого пола и чистых стен; перед установкой контрольный замер после отделки.
2. Порядок: корпус выставить по уровню опорами цоколя → закрепить к стене по задней планке → навесить двери и фасады, отрегулировать зазоры → подогнать и закрепить компенсатор.
3. Анкеры — с шагом не более 500 мм, не ближе 50 мм от края планки; на ГКЛ только в закладную, установленную до обшивки.
4. Скрытые коммуникации под анкеры проверить детектором; трассы электрики по плану розеток.

**Допущения и предложения на листе**

Основа листа: размеры сняты со скана обмерного плана KV оформление (см): часть подписей не читается, помещения выровнены по читаемым размерам; контрольный обмер не выполнен (К-1); высота потолка 2650 мм принята по отметкам обмера (Н = 2,50…2,66 м, ригель 2,28 м) — уточнить при обмере (К-2); толщины стен 300 / 120 мм приняты, межквартирная стена и колонны — по скану, не замерены (К-1); разрешённая мощность 15 кВт принята по типовым ТУ; при объединении двух квартир — переоформление ТУ (К-4); подрайон климата не задан — принят не северный (жилые от 2,5 м) (К-8).
См. лист открытых вопросов (лист 6, записи К-1, К-2, К-4, К-8).

1000 мм · печать 1:1

| Изм. | Кол.уч | Лист | № док. | Подп. | Дата |
|---|---|---|---|---|---|
| Разраб. | | Кырлан А.С. | | | 04.11.26 |
| Пров. | | | | | |
| ГИП | | | | | |
| | | | | | |
| Н. контр. | | | | | |
| Утв. | | | | | |

**ГД-2026-009-АИ**

Квартира 103 м²

Общая площадь 100,72* м² · * размеры со скана, не замерены (реестр — л. 6, 7, К-1)

Дизайн-проект интерьера

| Стадия | Лист | Листов |
|---|---|---|
| РП | 76 | 120 |

**Шкафы. Монтажная схема**

М 1:50

**Кырлан Александр Сергеевич**

выпуск 04.11.2026 № 35b47f1c2a · стр. 84 из 130

# Ведомости изделий, техники и фурнитуры

встроенная мебель и кухонный гарнитур · размеры в мм

## Ведомость изделий

| Марка | Наименование | Пом. | Ш×Г×В, мм | Корпус | Фасад | Кромка, мм | Кол. |
|---|---|---|---|---|---|---|---|
| Кл1 | Система хранения | 2 | 1500×400×2400 | ЛДСП декор «орех» 16 | без фасадов | 0,4 / 2 | 1 |
| П1 | Шкаф-купе | 4 | 3300×600×2450 | ЛДСП 16 | МДФ, шпон ореха 10 мм, масло матовое в профиле: латунь | 0,4 / 2 | 1 |
| Пс1 | Система хранения | 7 | 500×300×2000 | ЛДСП 16 | без фасадов | 0,4 / 2 | 1 |
| С2 | Шкаф распашной | 8 | 1800×600×2400 | ЛДСП 16 | МДФ, шпон ореха 18 мм, масло матовое | 0,4 / 2 | 1 |
| М4 | Шкаф распашной | 10 | 2000×600×2400 | ЛДСП 16 | МДФ, шпон ореха 18 мм, масло матовое; вставка — латунь | 0,4 / 2 | 1 |
| Кх1 | Модуль нижний: мойка | 5 | 800×600×900 | ЛДСП 16 | МДФ, шпон ореха 18 мм, масло матовое | 0,4 / 2 | 1 |
| Кх2 | Модуль под ПММ 60: без корпуса, фасад на дверь машины | 5 | 600×600×900 | без корпуса | МДФ 18 мм, эмаль матовая — на дверь машины (навеска из её комплекта), цоколь | | 1 |
| Кх3 | Модуль нижний: ящики | 5 | 600×600×900 | ЛДСП 16 | МДФ 18 мм, эмаль матовая | 0,4 / 2 | 1 |
| Кх4 | Модуль нижний: духовой шкаф, варочная | 5 | 800×600×900 | ЛДСП 16 | МДФ 18 мм, эмаль матовая | 0,4 / 2 | 1 |
| Кх8** | Модуль навесной: полки | 5 | 600×400×600 | ЛДСП 16 | МДФ 18 мм, эмаль матовая | 0,4 / 2 | 1 |
| Кх7 | Модуль нижний: ящики | 5 | 500×600×900 | ЛДСП 16 | МДФ 18 мм, эмаль матовая | 0,4 / 2 | 1 |
| Кх5 | Пенал: холодильник встр. | 5 | 600×650×2100 | ЛДСП 16 | МДФ эмаль 18 мм, матовая; цвет — тип | 0,4 / 2 | 1 |

## Ведомость встраиваемой техники

| Поз. | Прибор | Ниша, вырез, мм | Вентиляция | Питание | Схема |
|---|---|---|---|---|---|
| Кх1 | Мойка врезная / подстольная с сифоном | вырез по шаблону, ориентир 700 × 480 | | смеситель — выводы ВК | по модели |
| Кх2 | Посудомоечная машина встраиваемая, 60 см | ниша 600 × 862 (от пола до низа столешницы) | зазор в цоколе, по схеме | Р26: Кх3, Н=300 — в соседнем модуле, за ящиком | по модели |
| Кх4 | Духовой шкаф встраиваемый, 60 см | ниша 560 × 600, глубина ≥ 550 | зазор за шкафом, вырез в задней стенке | ЭВ2: Кх4, Н=150 — под духовым шкафом, доступ через ящик | по модели |
| Кх4 | Варочная панель индукционная, 60 см | вырез в столешнице 560 × 490 | | ЭВ1: Кх7, Н=600 — в соседнем модуле, за ящиком | по модели |
| Кх5 | Холодильник встраиваемый, ниша 1780 | ниша 1780 × 560 × 550 | решётка в цоколе, канал за корпусом, выход сверху | Р20**: Кх5, Н=2000 — над нишей холодильника, съёмная панель | по модели |
| Кх8** | Вытяжка встраиваемая в навесной модуль, 60 см | низ ≥ 650 над панелью | воздуховод к вентканалу, короб до потолка | Р21: Кх8**, Н=2250 — в навесном модуле | по модели |

## Ведомость фурнитуры

| № | Фурнитура | Тип, размер | Изделия | Кол. |
|---|---|---|---|---|
| 1 | Полкодержатель с фиксацией | ø5 мм | Кл1, П1, Пс1, С2, М4, Кх8**, Кх5 | 136 |
| 2 | Штанга выдвижная торцевая | L по глубине | Кл1 | 1 |
| 3 | Опора регулируемая с цоколем на клипсах | ход 20 мм | Кл1, П1, Пс1, С2, М4 | 38 |
| 4 | Анкер по основанию стены | по таблице крепежа | Кл1, П1, Пс1, С2, М4, Кх8** | 32 |
| 5 | Уголок крепления к стене от опрокидывания | стальной | Кл1, П1, Пс1, С2, М4, Кх5 | 12 |
| 6 | Система дверей купе: профиль, направляющие, ролики | на 4 двери | П1 | 1 |
| 7 | Ручка-профиль вертикальная | в цвет профиля | П1 | 4 |
| 8 | Штанга овальная 30×15, L = 817 | + 2 держателя | П1 | 1 |
| 9 | Полка для обуви выдвижная наклонная | ширина 817 | П1 | 3 |
| 10 | Полка для обуви выдвижная наклонная | ширина 794 | П1 | 3 |
| 11 | Штанга овальная 30×15, L = 794 | + 2 держателя | П1 | 1 |
| 12 | Петля накладная 110° с доводчиком | чашка 35 мм | С2, М4, Кх1, Кх8**, Кх5 | 63 |
| 13 | Штанга овальная 30×15, L = 876 | + 2 держателя | С2 | 1 |
| 14 | Штанга овальная 30×15, L = 976 | + 2 держателя | М4 | 1 |
| 15 | Ручка-профиль | латунь матовая | Кх1, Кх2, Кх3, Кх4, Кх8**, Кх7, Кх5 | 15 |
| 16 | Опора кухонная регулируемая 100–120 мм | + клипса цоколя | Кх1, Кх3, Кх4, Кх7, Кх5 | 24 |
| 17 | Комплект навески фасада ПММ | из поставки машины | Кх2 | 1 |
| 18 | Направляющие полного выдвижения с доводчиком NL 500 | пара | Кх3, Кх4, Кх7 | 7 |
| 19 | Навес регулируемый для навесного шкафа | пара на секцию | Кх8** | 1 |
| 20 | Шина монтажная | L = 540 | Кх8** | 1 |

## Примечания

1. Модели техники выбирает заказчик до изготовления мебели; ниши, вырезы и вентиляция — по монтажной схеме выбранной модели (условие гарантии), её номер вносится в ведомость.
2. Количество фурнитуры — по чертежам изделий; запас крепежа 5 %. Аналоги — по характеристикам (доводчик, нагрузка, ход).
3. Цвет корпусов, фасадов и профилей — по колерной карте проекта. Кромка — скрытые / видимые торцы, мм.

**Допущения и предложения на листе**

Основа листа: размеры сняты со скана обмерного плана KV оформление (см): часть подписей не читается, помещения выровнены по читаемым размерам; контрольный обмер не выполнен (К-1); высота потолка 2650 мм принята по отметкам обмера (Н = 2,50…2,66 м, ригель 2,28 м) — уточнить при обмере (К-2); толщины стен 300 / 120 мм приняты, межквартирная стена и колонны — по скану, не замерены (К-1); разрешённая мощность 15 кВт принята по типовым ТУ; при объединении двух квартир — переоформление ТУ (К-4); подрайон климата не задан — принят не северный (жилые от 2,5 м) (К-8).

Знак «**» — предложение проектировщика, заказчиком не утверждено (согласовать с заказчиком): Кх8 — над индукционной панелью Кх4 нужна вытяжка: в составе кухни её не было, розетка вытяжки образца висела без потребителя; Р20 — высота 2000 мм выше нормы 1 м (ПУЭ 6.6.30) по назначению: розетка встроенного прибора — в колонне Кх5 над нишей, в антресоли за съёмной панелью.

См. лист открытых вопросов (лист 6, записи К-1, К-2, К-4, К-8).

| Изм. | Кол.уч | Лист | № док. | Подп. | Дата |
|---|---|---|---|---|---|
| Разраб. | | Кырлан А.С. | | | 04.11.26 |
| Пров. | | | | | |
| ГИП | | | | | |
| | | | | | |
| Н. контр. | | | | | |
| Утв. | | | | | |

**ГД-2026-009-АИ**

Квартира 103 м²

Общая площадь 100,72* м² · * размеры со скана, не замерены (реестр — л. 6, 7, К-1)

Дизайн-проект интерьера

| Стадия | Лист | Листов |
|---|---|---|
| РП | 77 | 120 |

**Ведомости изделий, техники и фурнитуры**

М б/м

**Кырлан Александр Сергеевич**

09

# Развёртки и узлы

Кырлан Александр Сергеевич

выпуск 04.11.2026 № 35b47f1c2a · стр. 86 из 130

# Реестр марок отделки и позиций альбома

Реестр марок отделки (О ↔ позиции колерной карты) и марки позиций по видам

## Реестр марок отделки альбома

| Марка | Поверхность | Материал, изделие | Цвет, код | Помещения | Колер. карта |
|---|---|---|---|---|---|
| О1 | стены | окраска, Farrow & Ball Modern Emulsion, матовая, подготовка Q3 | Farrow & Ball No. 291 «School House White тёплый меловой белый» | 1, 3, 4, 5, 8, 9, 10 | К1 |
| О2 | акцентная стена | окраска, Farrow & Ball Modern Emulsion, матовая, подготовка Q3 | Farrow & Ball No. 289 «Inchyra Blue — тёмный сине-серый» | 1, 8, 10 | К2 |
| О3 | плинтус | плинтус МДФ, h 83 мм, Ultrawood Base 5340, ЛДФ под окраску, 83×15 мм, 2440 мм (арт. LDF-BASE-5340) | Farrow & Ball No. 291 «School House White тёплый меловой белый» | 1, 3, 4, 5, 8, 9, 10 | К4, К8 |
| О4 | потолок | окраска, Tikkurila Anti-Reflex 2, глубокоматовая, подготовка Q3 | NCS S 0502-Y «Белый с лёгкой желтизной» | 1, 2, 4, 7, 8, 9, 10 | К3 |
| О5 | пол | инженерная доска, Coswick Вековые традиции, 2100×127 мм, 1167-4250 | | 1, 2, 3, 5, 7, 8, 9, 10 | КМ1 |
| О6 | стены | окраска, Tikkurila Harmony, матовая, подготовка Q3 | NCS S 0502-Y «Белый с лёгкой желтизной» | 2, 7 | К5 |
| О7 | плинтус | плинтус МДФ, h 83 мм, Ultrawood Base 5340, ЛДФ под окраску, 83×15 мм, 2440 мм (арт. LDF-BASE-5340) | NCS S 0502-Y «Белый с лёгкой желтизной» | 2, 7 | К6 |
| О8 | акцентная стена | окраска, Farrow & Ball Modern Emulsion, аналог: интерьерная краска Farrow & Ball Modern Emulsion в цвете веера No. 255, матовая, матовая, подготовка К3 | Farrow & Ball No. 255 «Tanner's Brown тёмный шоколад» | 3 | К7 |
| О9 | потолок | окраска, Farrow & Ball Modern Emulsion, матовая, подготовка Q3 | Farrow & Ball No. 291 «School House White тёплый меловой белый» | 3, 5 | К1 |
| О10 | пол | керамогранит, Atlas Concorde Marvel Travertine, 600×1200×9 мм, A8UZ, затирка CG2WA | Atlas Concorde A8UZ «Marvel Travertine» | 4 | КМ2 |
| О11 | фартук | керамогранит, аналог: керамогранит матовый, тон F497, затирка CG2WA | #F1F1EC «тон Paper F497» | 5 | КМ3 |
| О12 | стены | облицовка плиткой, Atlas Concorde Marvel Travertine, 600×1200×9 мм, A8UZ, затирка CG2WA | Atlas Concorde A8UZ «Marvel Travertine» | 6, 11 | КМ4 |
| О13 | потолок | окраска, Tikkurila Luja 7, матовая, подготовка Q3 | NCS S 0502-Y «Белый с лёгкой желтизной» | 6, 11 | К9 |
| О14 | пол | керамогранит, 600×600×9 мм, Atlas Concorde Marvel Travertine Sand Cross 60×60 Matte Sensitech, арт. AFUL (той же коллекции, что стены A8UZ; тон сверить по образцу), затирка CG2WA | | 6, 11 | КМ5 |

## Марки позиций альбома по видам

| Префикс | Что обозначает, позиции | Листы |
|---|---|---|
| Д | двери: Д-1–Д-9 | 14–17 |
| ПР | проёмы без полотна (порталы): ПР-1 | 14–17 |
| ОК | окна: ОК-1–ОК-7 | 14–17 |
| Б, Г, Кл, Кх, М, П, Пс, С | мебель и оборудование: Б1–Б4, Г1–Г6, Кл1, Кх1–Кх7, Кх8**, М1–М6, П1–П3, Пс1, С1–С3 | 18–22 |
| Пм, См, Сн | сантехнические приборы: Пм1, См1–См4, Сн1–Сн4 | 33–42 |

Допущения и предложения на листе. Знак «*» принято (замерить). Знак «**» предложено (согласовать): плинтус пом. 1–5, 7–10, акцент пом. 3, фартук пом. 5, пол пом. 6, 11. См. лист открытых вопросов (лист 6).

## Марки позиций альбома по видам (продолжение)

| Префикс | Что обозначает, позиции | Листы |
|---|---|---|
| ДК | декор (картины, зеркала, растения): ДК1–ДК9 | 1, 61–65 |
| Т | текстиль (шторы, ковры): Т1–Т24 | 1, 61–65 |
| S | выключатели: S1, S2**, S3–S16 | 23–30 |
| Р | розетки: Р1–Р6, Р8**, Р11, Р13–Р16, Р17**, Р20**, Р21–Р23, Р26, Р33**, Р34–Р37, Р39, Р41–Р44, Р47, Р48, Р49**, Р50, Р51 | 23–30 |
| Св | светильники: Св1–Св9, Св10**, Св11–Св14, Св15**, Св16–Св22, Св23**, Св26–Св29, Св30**, Св31–Св39, Св50, Св51, Св52**, Св53–Св61, Св62**, Св64–Св72, Св73**, Св74 | 23–30 |
| БП | блоки питания LED: БП1–БП6 | 23–30 |
| ИП | извещатели: ИП1–ИП4, ИП6–ИП8 | 23–30 |
| LAN | розетки компьютерные: LAN1, LAN3, LAN4, LAN5** | 23–30 |
| ТВ | розетки ТВ: ТВ1 | 23–30 |
| ЩК, ЩС** | щиты: ЩК, ЩС** | 23–30 |
| ДФ | домофон: ДФ1 | 23–30 |
| АР | точки доступа Wi-Fi: АР1** | 23–30 |
| ЭВ | выводы кабеля: ЭВ1, ЭВ2, ЭВ4**, ЭВ5**, ЭВ6**, ЭВ7** | 23–30 |
| КУП | электроустановочные изделия: КУП1**, КУП2** | 23–30 |
| Ст В1, Ст К1, Ст К1-2 (кухня), Ст К1-4 (постирочная), Ст Т3 | стояки (системы В1, Т3, К1): Ст В1-1, Ст В1-2, Ст В1-3*, Ст В1-4, Ст К1-1, Ст К1-2 (кухня), Ст К1-3*, Ст К1-4 (постирочная), Ст Т3-1, Ст Т3-2, Ст Т3-3*, Ст Т3-4 | 33–42 |
| О | марки отделки (реестр альбома): О1–О14 | 2–5, 78–113 |
| К, КМ | позиции колерной карты: К1–К9, КМ1–КМ5 | 57–60 |
| РО | радиаторы отопления: РО-1–РО-7 | 31, 32 |

## Примечания

1. Марка отделки О — одна на весь альбом: одна и та же отделка (материал, изделие, цвет, формат) на всех листах имеет одну марку; на развёртках и планах стоят марки этого реестра.
2. Столбец «Колер. карта» — позиции колерной карты (лист 57): К — окраска по коду цвета, КМ — материал без кода цвета; «Помещения» — номера по экспликации; количества — по ведомости отделки помещений (лист 54).
3. Марки позиций: один префикс — один вид позиций на весь альбом (двери Д, окна ОК, мебель М, сантехприборы П, декор ДК, текстиль Т, колерная карта К и КМ, радиаторы РО, розетки Р, выключатели S, светильники Св; стояки — «Ст» и система, например «Ст К1-1»). Совпадение префиксов у разных видов — замечание к исходным данным, при выпуске исправляется в модели.


| Изм. | Кол.уч | Лист | № док. | Подп. | Дата | ГД-2026-009-АИ | | | |
|---|---|---|---|---|---|---|---|---|---|
| | | | | | | Квартира 103 м² | | | |
| | | | | | | Общая площадь 100,72* м² · * размеры со скана, не замерены (реестр — л. 6, 7, К-1) | | | |
| Разраб. | | Кырлан А.С. | | | 04.11.26 | Дизайн-проект интерьера | Стадия | Лист | Листов |
| Пров. | | | | | | | РП | 78 | 120 |
| ГИП | | | | | | | | | |
| Н. контр. | | | | | | Реестр марок отделки и позиций альбома | Кырлан Александр Сергеевич | | |
| Утв. | | | | | | М б/м | | | |

выпуск 04.11.2026 № 35b47f1c2a · стр. 87 из 130

# Схема расположения развёрток и узлов

План квартиры: марки развёрток по помещениям, выноски узлов, ведомость «марка → лист»



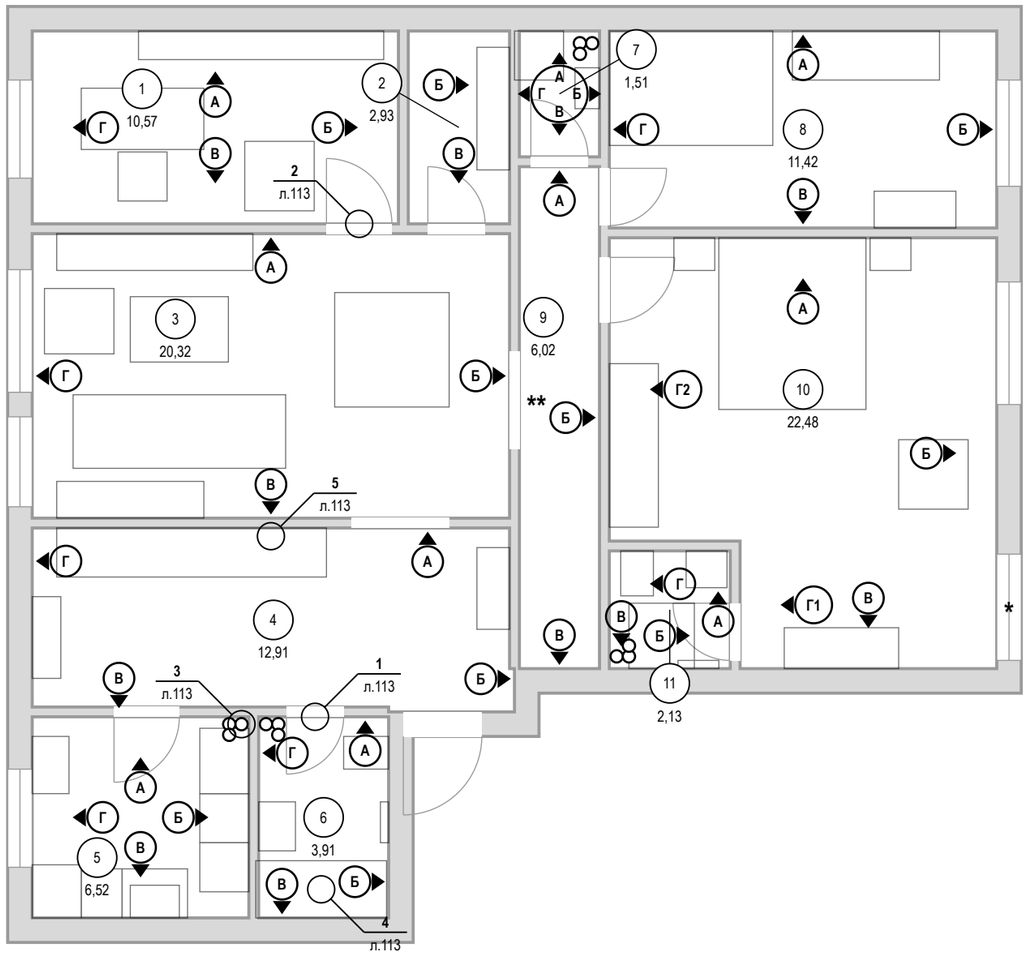


## Развёртки и узлы: марка → лист

| Марка | Помещение / узел | Лист |
|---|---|---|
| А, Б, В, Г | Кабинет-библиотека (пом. 1) | 80, 81 |
| Б, В | Кладовая (пом. 2) | 82 |
| А, Б, В, Г | Гостиная-столовая (пом. 3) | 83–87 |
| А, Б, В, Г | Прихожая-холл (пом. 4) | 88–91 |
| Б, В, А, Г | Кухня (пом. 5) | 92–94 |
| А, Б, В, Г | Ванная (пом. 6) | 95–97 |
| А, Б, В, Г | Постирочная (пом. 7) | 98 |
| А, Б, В, Г | Спальня 2 (пом. 8) | 99–101 |
| А, Б, В | Коридор (пом. 9) | 102–104 |
| А, Б, В, Г1, Г2 | Спальня мастер (пом. 10) | 105–109 |
| А, Б, В, Г | Ванная мастер (пом. 11) | 110–112 |
| узел 1 | Порог 15 мм: мокрая зона — смежное помещение | 113 |
| узел 2 | Дверь скрытого монтажа в плоскости стены, плинтус | 113 |
| узел 3 | Короб стояков К1-1, К1-2 (кухня) с люком и звукоизоляцией | 113 |
| узел 4 | Гидроизоляция санузла: заход на стены 200 мм, примыкание ванны | 113 |
| узел 5 | Плинтус МДФ 83×15 мм у окрашенной стены по доске (ламинату) | 113 |
| узел 6 | Плинтус МДФ 83×15 мм у окрашенной стены по керамограниту (плитке) | 113 |

**Допущения и предложения на листе**

Основа листа: размеры сняты со скана обмерного плана KV оформление (см): часть подписей не читается, помещения выровнены по читаемым размерам; контрольный обмер не выполнен (К-1); высота потолка 2650 мм принята по отметкам обмера (Н = 2,50…2,66 м, ригель 2,28 м) — уточнить при обмере (К-2); толщины стен 300 / 120 мм приняты, межквартирная стена и колонны — по скану, не замерены (К-1); разрешённая мощность 15 кВт принята по типовым ТУ; при объединении двух квартир — переоформление ТУ (К-4); подрайон климата не задан — принят не северный (жилые от 2,5 м) (К-8).

Знак «*» — принято, не замерено и не подтверждено (замерить на объекте): К-1: окно пом. 10 (стена Б) — Окно 1300 при смещение 3500 на стене Б основной части (длина 3830) выходило за стену на 970 мм; К-6: Ст К1-3, Ст В1-3, Ст Т3-3 — положение снято со скана обмера, отдельно не замерялось; ось внутри габарита поддона См1 — обмер угла по К-6.

Знак «**» — предложение проектировщика, заказчиком не утверждено (согласовать с заказчиком): К-5: дверь пом. 3 (стена Б) — проём в межквартирной стене — объединение квартир, предложение до техзаключения.

См. лист открытых вопросов (лист 6, записи К-1, К-2, К-4–К-6, К-8).

## Условные обозначения

- А — марка развёртки: буква стены, стрелка — взгляд
- выноска узла: над полкой — узел, под полкой — лист
- 1 — номер помещения, площадь м²

1000 мм · печать 1:1

## Примечания

1. Развёртки — вид на стену изнутри помещения; буквы стен — одна система на весь альбом (как на листах выводов, плитки и отделки).
2. Стены без электроточек, мебели, декора и акцентной отделки развёрток не имеют: их отделка — по ведомости отделки помещений.
3. Узлы — на листе узлов; места применения — по выноскам этого листа и ведомости «марка → лист».

| Изм. | Кол.уч | Лист | № док. | Подп. | Дата | ГД-2026-009-АИ | | | |
|---|---|---|---|---|---|---|---|---|---|
| | | | | | | Квартира 103 м² | | | |
| | | | | | | Общая площадь 100,72* м² · * размеры со скана, не замерены (реестр — л. 6, 7, К-1) | | | |
| Разраб. | | Кырлан А.С. | | | 04.11.26 | Дизайн-проект интерьера | Стадия | Лист | Листов |
| Пров. | | | | | | | РП | 79 | 120 |
| ГИП | | | | | | | | | |
| Н. контр. | | | | | | Схема расположения развёрток и узлов | Кырлан Александр Сергеевич | | |
| Утв. | | | | | | М 1:75 | | | |


выпуск 04.11.2026 № 35b47f1c2a · стр. 88 из 130

# Развёртки стен А, Б. Кабинет-библиотека (пом. 1)

Кабинет-библиотека (пом. 1) · вид изнутри помещения · размеры в мм, отметки в м


ПРЕДВАРИТЕЛЬНО · не для производства работ · открыто пунктов: 8 (реестр — л. 6, 7)

## Развёртка стены А

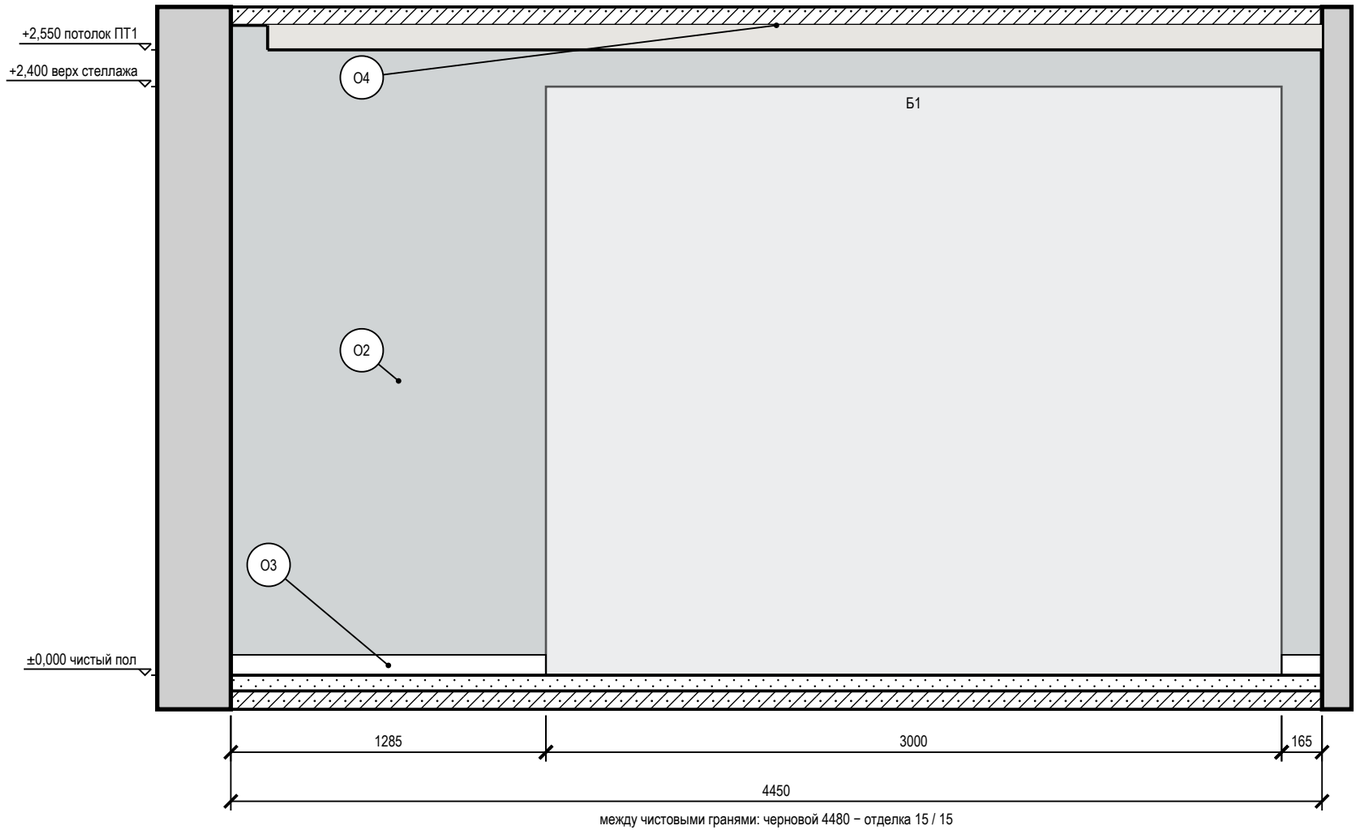



между чистовыми гранями: черновой 4480 − отделка 15 / 15

## Развёртка стены Б

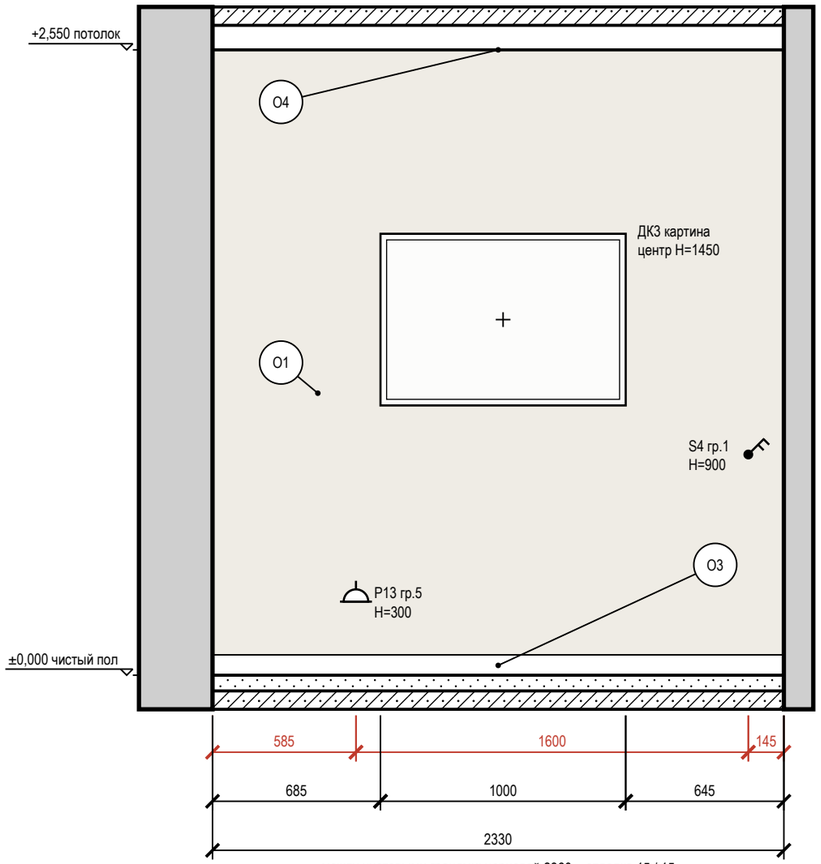


между чистовыми гранями: черновой 2360 − отделка 15 / 15

## Схема развёрток (М 1:100)

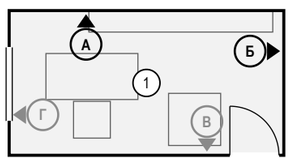


## Условные обозначения

- розетка с заземляющим контактом; у знака — марка, ×N постов в рамке, гр. — группа щита, Н — высота оси, мм
- выключатель одноклавишный
- выключатель двухклавишный (флажков — по числу клавиш)
- привязки точек и выводов от угла и от пола, мм
- мебель и приборы — фасад по расстановке (условно)
- картина (декор): марка Д, крест — центр, Н — высота центра, мм
- стены и перекрытия в сечении
- окраска: тон — цвет по коду производителя (условно)
- О1 — марка отделки по реестру отделки альбома
- А — марка развёртки: буква стены, стрелка — взгляд

**Допущения и предложения на листе**

Основа листа: размеры сняты со скана обмерного плана KV оформление (см): часть подписей не читается, помещения выровнены по читаемым размерам; контрольный обмер не выполнен (К-1); высота потолка 2650 мм принята по отметкам обмера (Н = 2,50…2,66 м, ригель 2,28 м) — уточнить при обмере (К-2); толщины стен 300 / 120 мм приняты, межквартирная стена и колонны — по скану, не замерены (К-1); разрешённая мощность 15 кВт принята по типовым ТУ; при объединении двух квартир — переоформление ТУ (К-4); подрайон климата не задан — принят не северный (жилые от 2,5 м) (К-8).

См. лист открытых вопросов (лист 6, записи К-1, К-2, К-4, К-8).

## Примечания

1. Развёртки — вид на стену изнутри помещения, по часовой стрелке; расположение — на схеме листа и на листе 79; размеры — в мм по чистовым поверхностям; отметки — в м от ±0,000; высоты Н — от чистого пола помещения до оси изделия, у декора — до центра.
2. Красная цепочка — привязки электроточек и выводов по осям от угла чистовых стен; высота Н — у знака, от чистого пола до оси; высоты мебели, проёмов и границ отделки — колонкой отметок слева. Стена с 5 и более точками или с мелкими звеньями привязок показана двумя видами: архитектурная развёртка (мебель, отделка, проёмы, высоты) и вид «Привязки» на отдельном листе — точки и выводы с марками, одна цепочка по осям и таблица привязок (каждая точка — строка).
3. У знака электроточки: марка (Р — розетка, S — выключатель, Св — светильник, ЭВ — вывод кабеля), ×N — число постов в рамке, гр. — группа щита, Н — высота оси от чистого пола, мм; группы по клавишам выключателя — на листе выключателей.
4. Схема мебели, приборов и декора не является технической документацией для производства мебели; габариты — по паспортам изделий.
5. Картины и зеркала крепить к основанию по паспорту изделия (закладные и анкеры — в перечне скрытых работ); крест — ось центра предмета.

1000 мм · печать 1:1

| Изм. | Кол.уч | Лист | № док. | Подп. | Дата |
|---|---|---|---|---|---|
| Разраб. | | Кырлан А.С. | | | 04.11.26 |
| Пров. | | | | | |
| ГИП | | | | | |
| Н. контр. | | | | | |
| Утв. | | | | | |

**ГД-2026-009-АИ**

Квартира 103 м²

Общая площадь 100,72* м² · * размеры со скана, не замерены (реестр — л. 6, 7, К-1)

Дизайн-проект интерьера

| Стадия | Лист | Листов |
|---|---|---|
| РП | 80 | 120 |

**Развёртки стен А, Б. Кабинет-библиотека (пом. 1)**

М 1:25

**Кырлан Александр Сергеевич**


выпуск 04.11.2026 № 35b47f1c2a · стр. 89 из 130

# Развёртки стен В, Г. Кабинет-библиотека (пом. 1)

Кабинет-библиотека (пом. 1) · вид изнутри помещения · размеры в мм, отметки в м


**ПРЕДВАРИТЕЛЬНО · не для производства работ · открыто пунктов: 8 (реестр — л. 6, 7)**

## Развёртка стены В

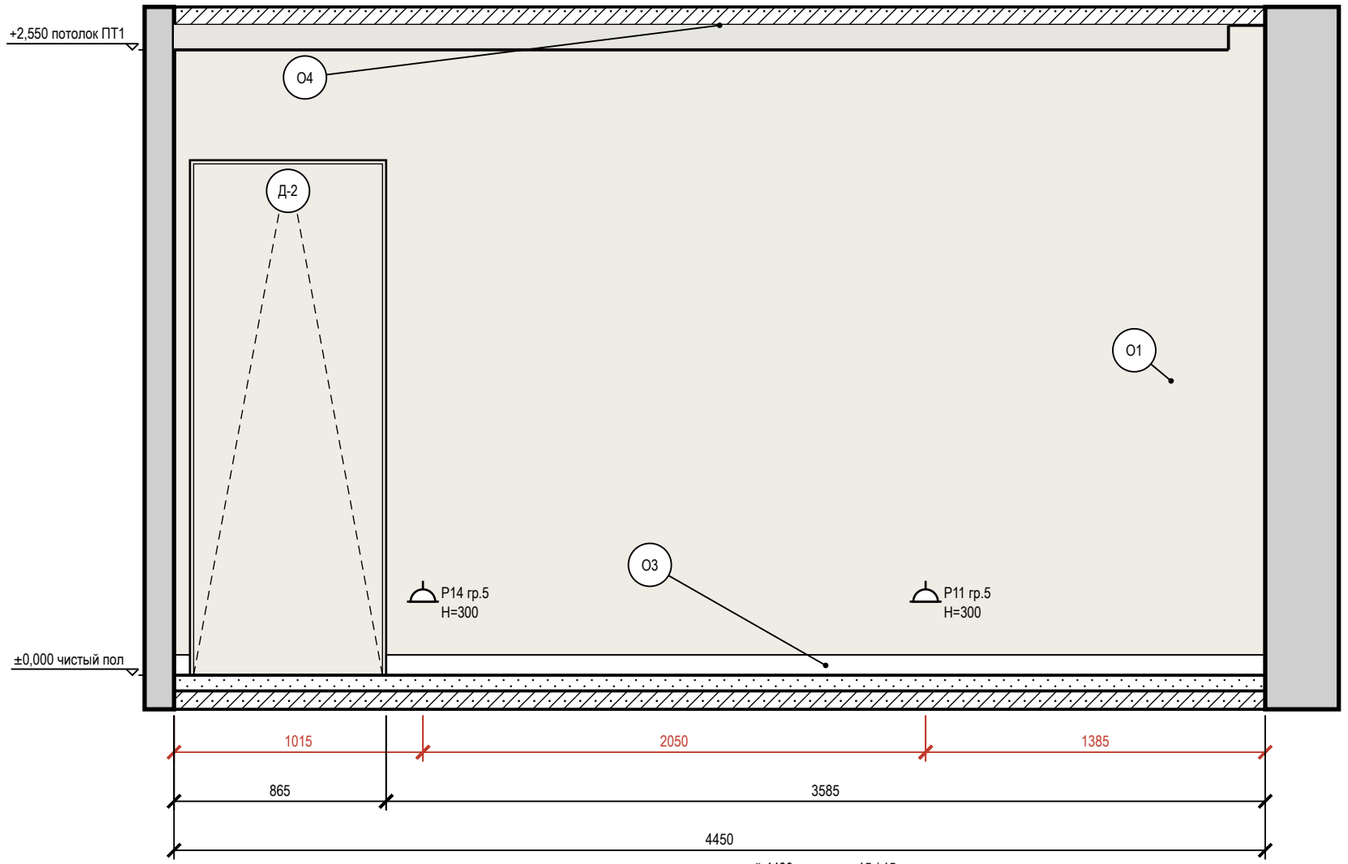



между чистовыми гранями: черновой 4480 − отделка 15 / 15

## Развёртка стены Г

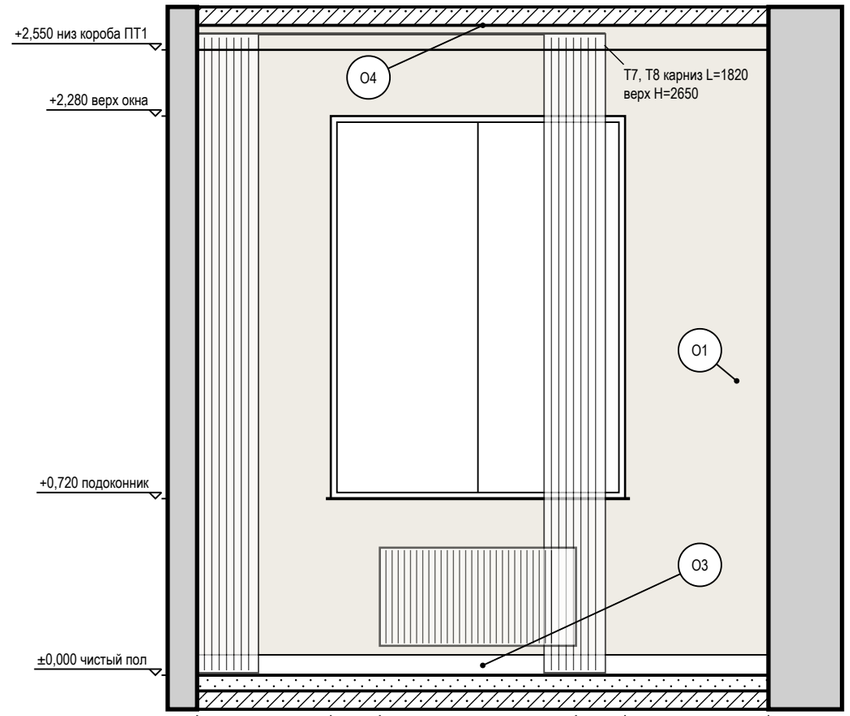


между чистовыми гранями: черновой 2360 − отделка 15 / 15

## Схема развёрток (М 1:100)

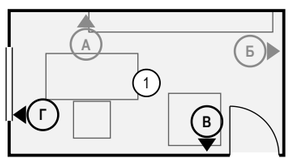


## Условные обозначения

- розетка с заземляющим контактом; у знака — марка, ×N постов в рамке, гр. — группа щита, Н — высота оси, мм
- привязки точек и выводов от угла и от пола, мм
- мебель и приборы — фасад по расстановке (условно)
- карниз (шина) и шторы в собранном виде: марка Т, длина L, верх Н
- дверь скрытого монтажа: полотно в плоскости стены (узел — на листе узлов)
- окно: проём, рама, подоконник
- радиатор отопления; марка — по плану отопления
- стены и перекрытия в сечении
- окраска: тон — цвет по коду производителя (условно)
- О1 — марка отделки по реестру отделки альбома
- А — марка развёртки: буква стены, стрелка — взгляд

**Допущения и предложения на листе**

Основа листа: размеры сняты со скана обмерного плана KV оформление (см): часть подписей не читается, помещения выровнены по читаемым размерам; контрольный обмер не выполнен (К-1); высота потолка 2650 мм принята по отметкам обмера (Н = 2,50…2,66 м, ригель 2,28 м) — уточнить при обмере (К-2); толщины стен 300 / 120 мм приняты, межквартирная стена и колонны — по скану, не замерены (К-1); разрешённая мощность 15 кВт принята по типовым ТУ; при объединении двух квартир — переоформление ТУ (К-4); подрайон климата не задан — принят не северный (жилые от 2,5 м) (К-8).

См. лист открытых вопросов (лист 6, записи К-1, К-2, К-4, К-8).

## Примечания

1. Развёртки — вид на стену изнутри помещения, по часовой стрелке; расположение — на схеме листа и на листе 79; размеры — в мм по чистовым поверхностям; отметки — в м от ±0,000; высоты Н — от чистого пола помещения до оси изделия, у декора — до центра.
2. Красная цепочка — привязки электроточек и выводов по осям от угла чистовых стен; высота Н — у знака, от чистого пола до оси; высоты мебели, проёмов и границ отделки — колонкой отметок слева. Стена с 5 и более точками или с мелкими звеньями привязок показана двумя видами: архитектурная развёртка (мебель, отделка, проёмы, высоты) и вид «Привязки» на отдельном листе — точки и выводы с марками, одна цепочка по осям и таблица привязок (каждая точка — строка).
3. У знака электроточки: марка (Р — розетка, S — выключатель, Св — светильник, ЭВ — вывод кабеля), ×N — число постов в рамке, гр. — группа щита, Н — высота оси от чистого пола, мм; группы по клавишам выключателя — на листе выключателей.
4. Схема мебели, приборов и декора не является технической документацией для производства мебели; габариты — по паспортам изделий.
5. Карнизы (шины) — по ведомости текстиля декоратора: длина L и верх Н на развёртке — те же числа, что в ведомости; крепление — до окраски потолка.
6. Двери скрытого монтажа — полотно в плоскости стены, отделка стены по полотну, плинтус прерывается у короба (узел — на листе узлов).
7. Карниз Т7, Т8: по ведомости текстиля шина L=1820 мм, а от её начала до чистового угла стены — 1665 мм: шина не встаёт, длину согласовать с декоратором до заказа.
8. Линии узора (швы плитки, складки штор, рёбра радиаторов) прерываются у знаков и выносок — просвет между линиями не менее 0,7 мм.

1000 мм · печать 1:1

| Изм. | Кол.уч | Лист | № док. | Подп. | Дата |
|---|---|---|---|---|---|
| Разраб. | | Кырлан А.С. | | | 04.11.26 |
| Пров. | | | | | |
| ГИП | | | | | |
| Н. контр. | | | | | |
| Утв. | | | | | |

**ГД-2026-009-АИ**

Квартира 103 м²

Общая площадь 100,72* м² · * размеры со скана, не замерены (реестр — л. 6, 7, К-1)

Дизайн-проект интерьера

| Стадия | Лист | Листов |
|---|---|---|
| РП | 81 | 120 |

**Развёртки стен В, Г. Кабинет-библиотека (пом. 1)**

М 1:25

**Кырлан Александр Сергеевич**


выпуск 04.11.2026 № 35b47f1c2a · стр. 90 из 130

# Развёртки стен. Кладовая (пом. 2)

Кладовая (пом. 2) · вид изнутри помещения · размеры в мм, отметки в м


ПРЕДВАРИТЕЛЬНО · не для производства работ · открыто пунктов: 8 (реестр — л. 6, 7)

## Развёртка стены Б

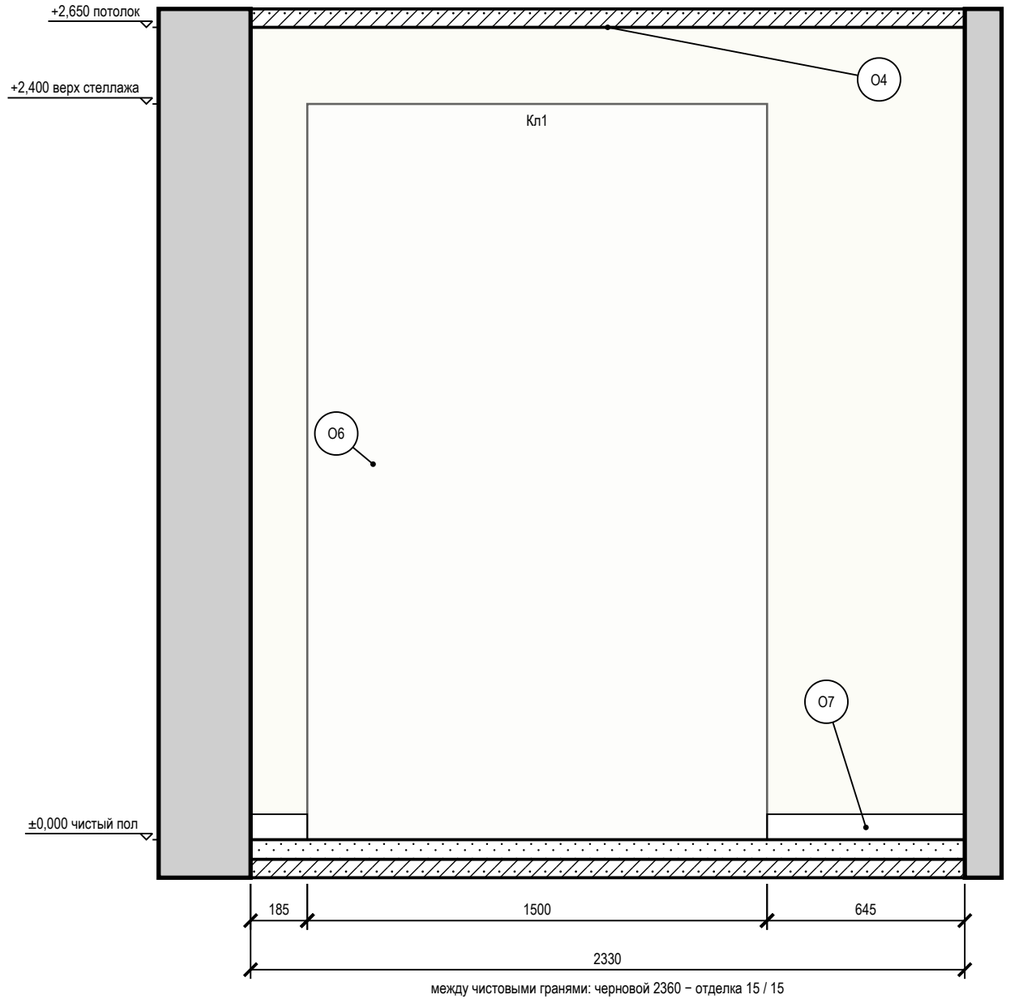



между чистовыми гранями: черновой 2360 − отделка 15 / 15

## Развёртка стены В

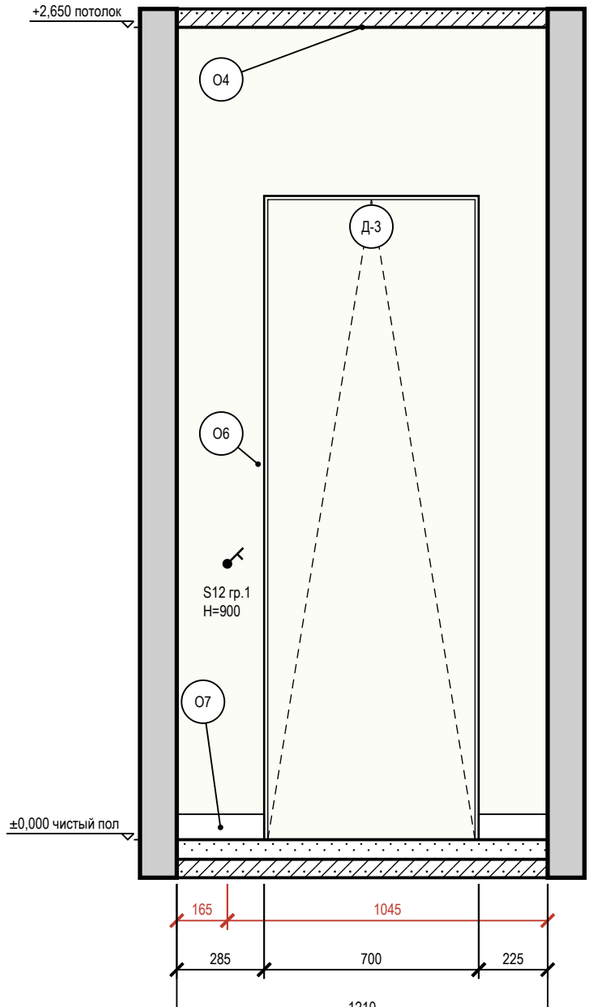


между чистовыми гранями: черновой 1240 − отделка 15 / 15

## Схема развёрток (М 1:100)

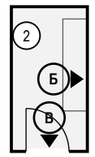


## Условные обозначения

- выключатель одноклавишный
- привязки точек и выводов от угла и от пола, мм
- мебель и приборы — фасад по расстановке (условно)
- дверь скрытого монтажа: полотно в плоскости стены (узел — на листе узлов)
- стены и перекрытия в сечении
- окраска: тон — цвет по коду производителя (условно)
- О1 — марка отделки по реестру отделки альбома
- А — марка развёртки: буква стены, стрелка — взгляд

## Ведомость отделки (на листе)

| Марка | Поверхность | Материал, изделие | Цвет, код | Кол. |
|---|---|---|---|---|
| О4 | потолок | окраска, Tikkurila Anti-Reflex 2, глубокоматовая, подготовка Q3 | NCS S 0502-Y «Белый с лёгкой желтизной» | 2,9 м² |
| О6 | стены | окраска, Tikkurila Harmony, матовая, подготовка Q3 | NCS S 0502-Y «Белый с лёгкой желтизной» | 7,9 м² |
| О7 | плинтус | плинтус МДФ, h 83 мм, Ultrawood Base 5340, ЛДФ под окраску, 83×15 мм, 2440 мм (арт. LDF-BASE-5340) | NCS S 0502-Y «Белый с лёгкой желтизной» | 1,3 м |

**Допущения и предложения на листе**

Основа листа: размеры сняты со скана обмерного плана KV оформление (см): часть подписей не читается, помещения выровнены по читаемым размерам; контрольный обмер не выполнен (К-1); высота потолка 2650 мм принята по отметкам обмера (Н = 2,50…2,66 м, ригель 2,28 м) — уточнить при обмере (К-2); толщины стен 300 / 120 мм приняты, межквартирная стена и колонны — по скану, не замерены (К-1); разрешённая мощность 15 кВт принята по типовым ТУ; при объединении двух квартир — переоформление ТУ (К-4); подрайон климата не задан — принят не северный (жилые от 2,5 м) (К-8).

См. лист открытых вопросов (лист 6, записи К-1, К-2, К-4, К-8).

## Примечания

1. Развёртки — вид на стену изнутри помещения, по часовой стрелке; расположение — на схеме листа и на листе 79; размеры — в мм по чистовым поверхностям; отметки — в м от ±0,000; высоты Н — от чистого пола помещения до оси изделия, у декора — до центра.
2. Красная цепочка — привязки электроточек и выводов по осям от угла чистовых стен; высота Н — у знака, от чистого пола до оси; высоты мебели, проёмов и границ отделки — колонкой отметок слева. Стена с 5 и более точками или с мелкими звеньями привязок показана двумя видами: архитектурная развёртка (мебель, отделка, проёмы, высоты) и вид «Привязки» на отдельном листе — точки и выводы с марками, одна цепочка по осям и таблица привязок (каждая точка — строка).
3. У знака электроточки: марка (Р — розетка, S — выключатель, Св — светильник, ЭВ — вывод кабеля), ×N — число постов в рамке, гр. — группа щита, Н — высота оси от чистого пола, мм; группы по клавишам выключателя — на листе выключателей.
4. Схема мебели, приборов и декора не является технической документацией для производства мебели; габариты — по паспортам изделий.
5. Двери скрытого монтажа — полотно в плоскости стены, отделка стены по полотну, плинтус прерывается у короба (узел — на листе узлов).

1000 мм · печать 1:1

| Изм. | Кол.уч | Лист | № док. | Подп. | Дата |
|---|---|---|---|---|---|
| Разраб. | | Кырлан А.С. | | | 04.11.26 |
| Пров. | | | | | |
| ГИП | | | | | |
| | | | | | |
| Н. контр. | | | | | |
| Утв. | | | | | |

**ГД-2026-009-АИ**

Квартира 103 м²

Общая площадь 100,72* м² · * размеры со скана, не замерены (реестр — л. 6, 7, К-1)

Дизайн-проект интерьера

| Стадия | Лист | Листов |
|---|---|---|
| РП | 82 | 120 |

**Развёртки стен. Кладовая (пом. 2)**

М 1:20

**Кырлан Александр Сергеевич**


выпуск 04.11.2026 № 35b47f1c2a · стр. 91 из 130

# Развёртка стены А. Гостиная-столовая (пом. 3)

Гостиная-столовая (пом. 3) · вид изнутри помещения · размеры в мм, отметки в м

**ПРЕДВАРИТЕЛЬНО · не для производства работ · открыто пунктов: 8 (реестр — л. 6, 7)**


## Развёртка стены А

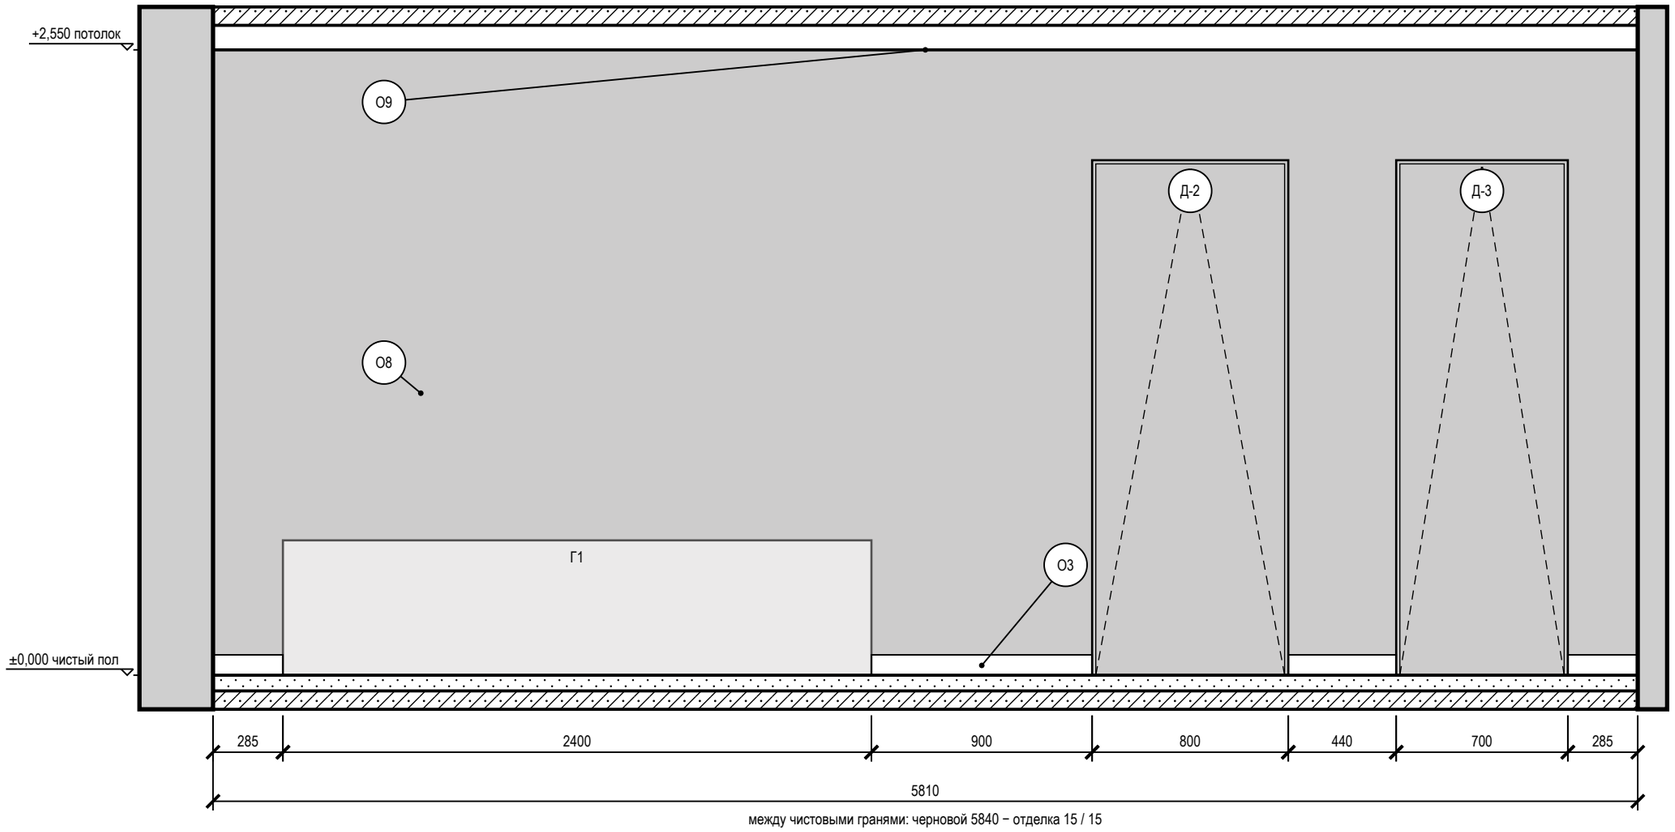


## Условные обозначения

- мебель и приборы — фасад по расстановке (условно)
- дверь скрытого монтажа: полотно в плоскости стены (узел — на листе узлов)
- стены и перекрытия в сечении
- окраска: тон — цвет по коду производителя (условно)
- О1 — марка отделки по реестру отделки альбома
- А — марка развёртки: буква стены, стрелка — взгляд

## Схема развёрток (М 1:100)

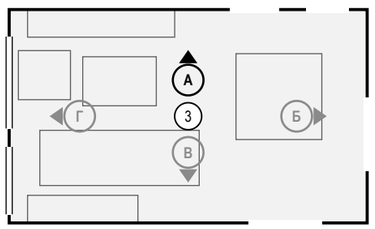


## Ведомость отделки (на листе)

| Марка | Поверхность | Материал, изделие | Цвет, код | Кол. |
|---|---|---|---|---|
| О3 | плинтус | плинтус МДФ, h 83 мм, Ultrawood Base 5340, ЛДФ под окраску, 83×15 мм, 2440 мм (арт. LDF-BASE-5340), полуглянцевая | Farrow & Ball No. 291 «School House White тёплый меловой белый» | 1,9 м |
| О8 | акцентная стена | окраска, Farrow & Ball Modern Emulsion, аналог: интерьерная краска Farrow & Ball Modern Emulsion в цвете веера No. 255, матовая, матовая, подготовка К3 | Farrow & Ball No. 255 «Tanner's Brown — тёмный шоколад» | 11,7 м² |
| О9 | потолок | окраска, Farrow & Ball Modern Emulsion, матовая, подготовка Q3 | Farrow & Ball No. 291 «School House White тёплый меловой белый» | 20,3 м² |

**Допущения и предложения на листе**

Основа листа: размеры сняты со скана обмерного плана KV оформление (см): часть подписей не читается, помещения выровнены по читаемым размерам; контрольный обмер не выполнен (К-1); высота потолка 2650 мм принята по отметкам обмера (Н = 2,50…2,66 м, ригель 2,28 м) — уточнить при обмере (К-2); толщины стен 300 / 120 мм приняты, межквартирная стена и колонны — по скану, не замерены (К-1); разрешённая мощность 15 кВт принята по типовым ТУ; при объединении двух квартир — переоформление ТУ (К-4); подрайон климата не задан — принят не северный (жилые от 2,5 м) (К-8).

Знак «**» — предложение проектировщика, заказчиком не утверждено (согласовать с заказчиком): К-5: дверь пом. 3 (стена Б) — проём в межквартирной стене — объединение квартир, предложение до техзаключения.

См. лист открытых вопросов (лист 6, записи К-1, К-2, К-4, К-5, К-8).

## Примечания

1. Развёртки — вид на стену изнутри помещения, по часовой стрелке; расположение — на схеме листа и на листе 79; размеры — в мм по чистовым поверхностям; отметки — в м от ±0,000; высоты Н — от чистого пола помещения до оси изделия, у декора — до центра.
2. Стена А показана двумя видами: здесь — архитектурная развёртка (мебель, отделка, проёмы, высоты), электроточки и выводы ВК с привязками и таблицей — на листе 84 («Привязки»).
3. Схема мебели, приборов и декора не является технической документацией для производства мебели; габариты — по паспортам изделий.
4. Двери скрытого монтажа — полотно в плоскости стены, отделка стены по полотну, плинтус прерывается у короба (узел — на листе узлов).

1000 мм · печать 1:1

| Изм. | Кол.уч | Лист | № док. | Подп. | Дата |
|---|---|---|---|---|---|
| Разраб. | | Кырлан А.С. | | | 04.11.26 |
| Пров. | | | | | |
| ГИП | | | | | |
| Н. контр. | | | | | |
| Утв. | | | | | |

**ГД-2026-009-АИ**

Квартира 103 м²

Общая площадь 100,72* м² · * размеры со скана, не замерены (реестр — л. 6, 7, К-1)

Дизайн-проект интерьера

| Стадия | Лист | Листов |
|---|---|---|
| РП | 83 | 120 |

**Развёртка стены А. Гостиная-столовая (пом. 3)**

М 1:25

**Кырлан Александр Сергеевич**


выпуск 04.11.2026 № 35b47f1c2a · стр. 92 из 130

# Привязки электроточек, стена А. Гостиная-столовая (пом. 3)

Гостиная-столовая (пом. 3) · вид изнутри помещения · привязки в мм, отметки в м · к развёртке на листе 83

ПРЕДВАРИТЕЛЬНО · не для производства работ · открыто пунктов: 8 (реестр — л. 6, 7)

## Развёртка стены А: электроточки и выводы

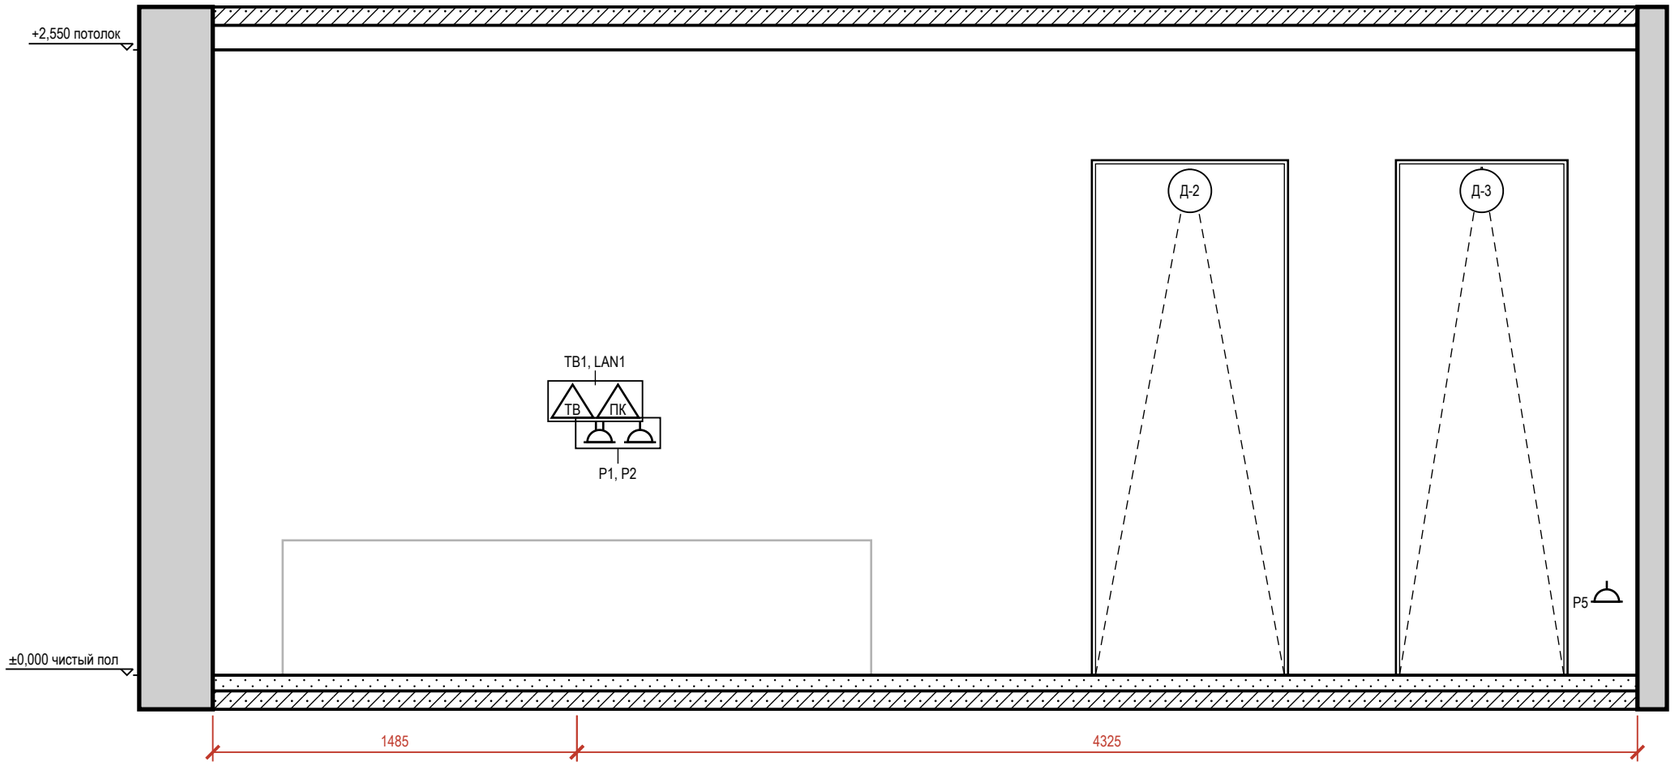



## Таблица привязок электроточек и выводов

| Марка | Назначение | От угла, мм | Н от пола, мм | Примечание |
|---|---|---|---|---|
| TB1 | розетка ТВ: ТВ-зона | 1485 | 1100 | |
| P1 | розетка: ТВ-зона: телевизор, медиаплеер | 1585 | 950 | рамка 2 поста, гр. 5 |
| LAN1 | розетка RJ45: ТВ-зона: Smart TV | 1635 | 1100 | |
| P2 | розетка: ТВ-зона: саундбар | 1735 | 950 | гр. 5 |
| P5 | розетка: обеденная зона, буфет Г6 | 5685 | 300 | гр. 5 |

## Условные обозначения

- розетка с заземляющим контактом; у знака — марка, ×N постов в рамке, гр. — группа щита, Н — высота оси, мм
- ПК — розетка компьютерная RJ45
- ТВ — розетка телевизионная
- привязки точек и выводов от угла и от пола, мм
- А — марка развёртки: буква стены, стрелка — взгляд

## Схема развёрток (М 1:200)

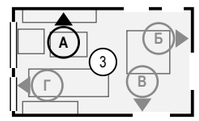


## Примечания

1. Вид «Привязки» стены А — электроточки и выводы ВК; архитектурная развёртка (мебель, отделка, проёмы, высоты) — на листе 83, расположение — на листе 79. Мебель и приборы — подложкой для ориентира; их марки и обозначения мебели, проёмов и стен — там же.
2. Привязки — в мм: по горизонтали от левого чистового угла стены до оси изделия, Н — от чистого пола до оси; все точки — в таблице привязок. Красная цепочка — привязки по осям; точки ближе 150 мм одна к другой в цепочку не дробятся — их привязки только в таблице.
3. У знака — марка электроточки (Р — розетка, S — выключатель, Св — светильник, ЭВ — вывод кабеля); посты в рамке и группа щита — в графе «Примечание»; группы по клавишам выключателя — на листе выключателей.

**Допущения и предложения на листе**

Основа листа: размеры сняты со скана обмерного плана KV оформление (см): часть подписей не читается, помещения выровнены по читаемым размерам; контрольный обмер не выполнен (К-1); высота потолка 2650 мм принята по отметкам обмера (Н = 2,50…2,66 м, ригель 2,28 м) — уточнить при обмере (К-2); толщины стен 300 / 120 мм приняты, межквартирная стена и колонны — по скану, не замерены (К-1); разрешённая мощность 15 кВт принята по типовым ТУ; при объединении двух квартир — переоформление ТУ (К-4); подрайон климата не задан — принят не северный (жилые от 2,5 м) (К-8).

Знак «**» — предложение проектировщика, заказчиком не утверждено (согласовать с заказчиком): К-5: дверь пом. 3 (стена Б) — проём в межквартирной стене — объединение квартир, предложение до техзаключения.

См. лист открытых вопросов (лист 6, записи К-1, К-2, К-4, К-5, К-8).

1000 мм · печать 1:1

| Изм. | Кол.уч | Лист | № док. | Подп. | Дата |
|---|---|---|---|---|---|
| Разраб. | | Кырлан А.С. | | | 04.11.26 |
| Пров. | | | | | |
| ГИП | | | | | |
| | | | | | |
| Н. контр. | | | | | |
| Утв. | | | | | |

**ГД-2026-009-АИ**

Квартира 103 м²

Общая площадь 100,72* м² · * размеры со скана, не замерены (реестр — л. 6, 7, К-1)

Дизайн-проект интерьера

| Стадия | Лист | Листов |
|---|---|---|
| РП | 84 | 120 |

**Привязки электроточек, стена А. Гостиная-столовая (пом. 3)**

М 1:25

**Кырлан Александр Сергеевич**


выпуск 04.11.2026 № 35b47f1c2a · стр. 93 из 130

# Развёртка стены Б. Гостиная-столовая (пом. 3)

Гостиная-столовая (пом. 3) · вид изнутри помещения · размеры в мм, отметки в м

ПРЕДВАРИТЕЛЬНО · не для производства работ · открыто пунктов: 8 (реестр — л. 6, 7)

## Развёртка стены Б

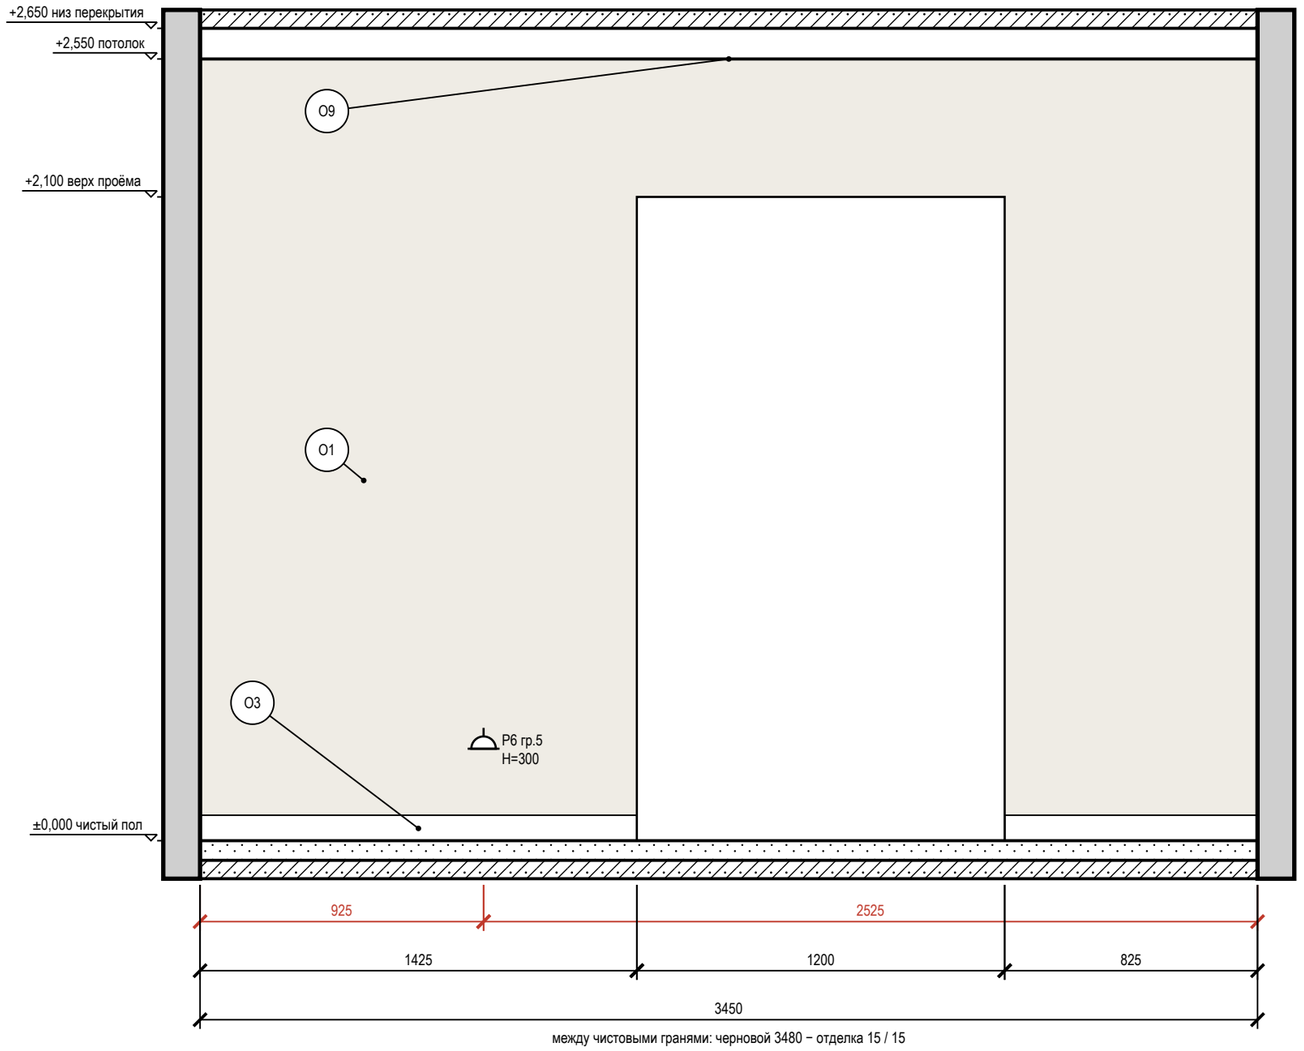


**Допущения и предложения на листе**

Основа листа: размеры сняты со скана обмерного плана KV оформление (см): часть подписей не читается, помещения выровнены по читаемым размерам; контрольный обмер не выполнен (К-1); высота потолка 2650 мм принята по отметкам обмера (Н = 2,50…2,66 м, ригель 2,28 м) — уточнить при обмере (К-2); толщины стен 300 / 120 мм приняты, межквартирная стена и колонны — по скану, не замерены (К-1); разрешённая мощность 15 кВт принята по типовым ТУ; при объединении двух квартир — переоформление ТУ (К-4); подрайон климата не задан — принят не северный (жилые от 2,5 м) (К-8).

Знак «**» — предложение проектировщика, заказчиком не утверждено (согласовать с заказчиком): К-5: дверь пом. 3 (стена Б) — проём в межквартирной стене — объединение квартир, предложение до техзаключения.


См. лист открытых вопросов (лист 6, записи К-1, К-2, К-4, К-5, К-8).

## Примечания

1. Развёртки — вид на стену изнутри помещения, по часовой стрелке; расположение — на схеме листа и на листе 79; размеры — в мм по чистовым поверхностям; отметки — в м от ±0,000; высоты Н — от чистого пола помещения до оси изделия, у декора — до центра.
2. Красная цепочка — привязки электроточек и выводов по осям от угла чистовых стен; высота Н — у знака, от чистого пола до оси; высоты мебели, проёмов и границ отделки — колонкой отметок слева. Стена с 5 и более точками или с мелкими звеньями привязок показана двумя видами: архитектурная развёртка (мебель, отделка, проёмы, высоты) и вид «Привязки» на отдельном листе — точки и выводы с марками, одна цепочка по осям и таблица привязок (каждая точка — строка).
3. У знака электроточки: марка (Р — розетка, S — выключатель, Св — светильник, ЭВ — вывод кабеля), ×N — число постов в рамке, гр. — группа щита, Н — высота оси от чистого пола, мм; группы по клавишам выключателя — на листе выключателей.
4. Схема мебели, приборов и декора не является технической документацией для производства мебели; габариты — по паспортам изделий.

1000 мм · печать 1:1

## Схема развёрток (М 1:100)

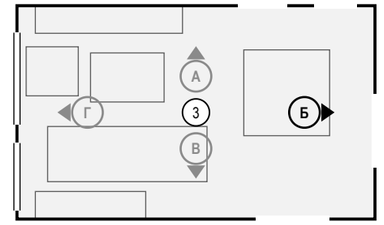


## Условные обозначения

- розетка с заземляющим контактом; у знака — марка, ×N постов в рамке, гр. — группа щита, Н — высота оси, мм
- привязки точек и выводов от угла и от пола, мм
- мебель и приборы — фасад по расстановке (условно)
- дверной проём; марка двери — в кружке
- стены и перекрытия в сечении
- окраска: тон — цвет по коду производителя (условно)
- О1 — марка отделки по реестру отделки альбома
- А — марка развёртки: буква стены, стрелка — взгляд

## Ведомость отделки (на листе)

| Марка | Поверхность | Материал, изделие | Цвет, код | Кол. |
|---|---|---|---|---|
| О1 | стены | окраска, Farrow & Ball Modern Emulsion, матовая, подготовка К3 | Farrow & Ball No. 291 «School House White — тёплый меловой белый» | 6,3 м² |
| О3 | плинтус | плинтус МДФ, h 83 мм, Ultrawood Base 5340, ЛДФ под окраску, 83×15 мм, 2440 мм (арт. LDF-BASE-5340), полуглянцевая | Farrow & Ball No. 291 «School House White — тёплый меловой белый» | 2,3 м |
| О9 | потолок | окраска, Farrow & Ball Modern Emulsion, матовая, подготовка Q3 | Farrow & Ball No. 291 «School House White — тёплый меловой белый» | 20,3 м² |

| Изм. | Кол.уч | Лист | № док. | Подп. | Дата |
|---|---|---|---|---|---|
| Разраб. | | Кырлан А.С. | | | 04.11.26 |
| Пров. | | | | | |
| ГИП | | | | | |
| | | | | | |
| Н. контр. | | | | | |
| Утв. | | | | | |

**ГД-2026-009-АИ**

Квартира 103 м²

Общая площадь 100,72* м² · * размеры со скана, не замерены (реестр — л. 6, 7, К-1)

| Дизайн-проект интерьера | Стадия | Лист | Листов |
|---|---|---|---|
| | РП | 85 | 120 |

**Развёртка стены Б. Гостиная-столовая (пом. 3)**

М 1:20

**Кырлан Александр Сергеевич**


выпуск 04.11.2026 № 35b47f1c2a · стр. 94 из 130

# Развёртка стены В. Гостиная-столовая (пом. 3)

Гостиная-столовая (пом. 3) · вид изнутри помещения · размеры в мм, отметки в м


**ПРЕДВАРИТЕЛЬНО · не для производства работ · открыто пунктов: 8 (реестр — л. 6, 7)**

## Развёртка стены В

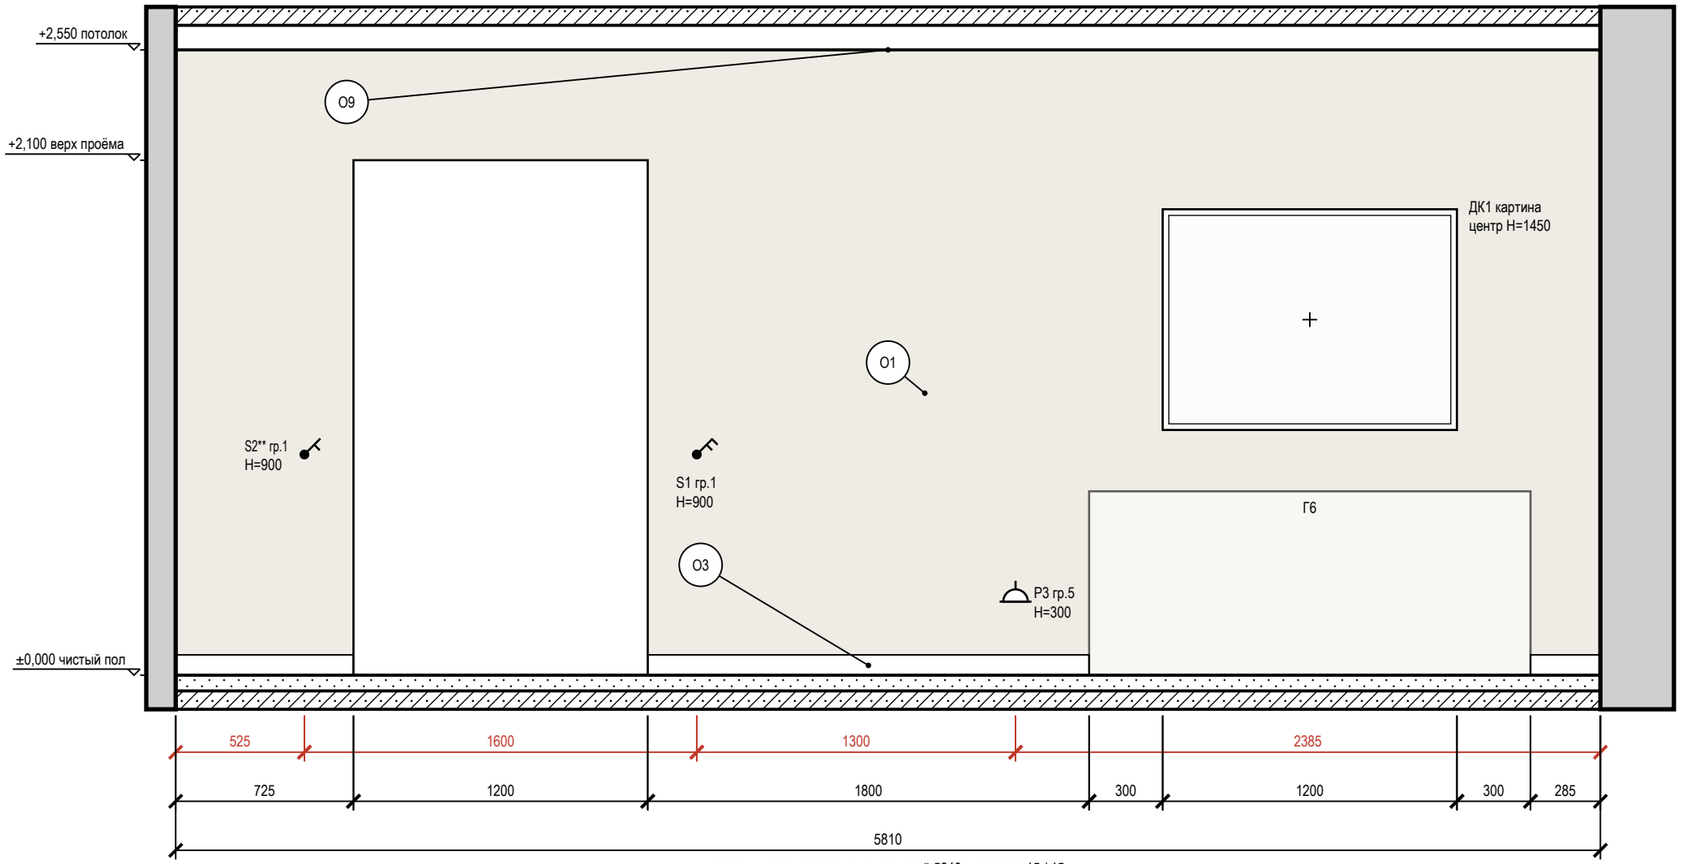


между чистовыми гранями: черновой 5840 − отделка 15 / 15

## Схема развёрток (М 1:100)

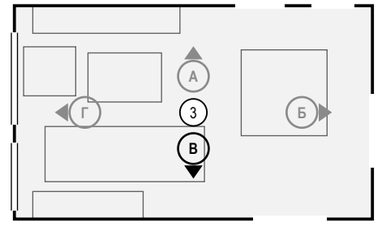


## Условные обозначения

- розетка с заземляющим контактом; у знака — марка, ×N постов в рамке, гр. — группа щита, Н — высота оси, мм
- выключатель одноклавишный
- выключатель двухклавишный (флажков — по числу клавиш)
- привязки точек и выводов от угла и от пола, мм
- мебель и приборы — фасад по расстановке (условно)
- картина (декор): марка Д, крест — центр, Н — высота центра, мм
- дверной проём; марка двери — в кружке
- стены и перекрытия в сечении
- окраска: тон — цвет по коду производителя (условно)
- О1 — марка отделки по реестру отделки альбома
- А — марка развёртки: буква стены, стрелка — взгляд

**Допущения и предложения на листе**

Основа листа: размеры сняты со скана обмерного плана KV оформление (см): часть подписей не читается, помещения выровнены по читаемым размерам; контрольный обмер не выполнен (К-1); высота потолка 2650 мм принята по отметкам обмера (Н = 2,50…2,66 м, ригель 2,28 м) — уточнить при обмере (К-2); толщины стен 300 / 120 мм приняты, межквартирная стена и колонны — по скану, не замерены (К-1); разрешённая мощность 15 кВт принята по типовым ТУ; при объединении двух квартир — переоформление ТУ (К-4); подрайон климата не задан — принят не северный (жилые от 2,5 м) (К-8).

Знак «**» — предложение проектировщика, заказчиком не утверждено (согласовать с заказчиком): S2 — светорегулятор добавлен под диммируемую ленту L3; уровни сценариев выбраны конвейером; К-5: дверь пом. 3 (стена Б) — проём в межквартирной стене — объединение квартир, предложение до техзаключения.

См. лист открытых вопросов (лист 6, записи К-1, К-2, К-4, К-5, К-8).

## Примечания

1. Развёртки — вид на стену изнутри помещения, по часовой стрелке; расположение — на схеме листа и на листе 79; размеры — в мм по чистовым поверхностям; отметки — в м от ±0,000; высоты Н — от чистого пола помещения до оси изделия, у декора — до центра.
2. Красная цепочка — привязки электроточек и выводов по осям от угла чистовых стен; высота Н — у знака, от чистого пола до оси; высоты мебели, проёмов и границ отделки — колонкой отметок слева. Стена с 5 и более точками или с мелкими звеньями привязок показана двумя видами: архитектурная развёртка (мебель, отделка, проёмы, высоты) и вид «Привязки» на отдельном листе — точки и выводы с марками, одна цепочка по осям и таблица привязок (каждая точка — строка).
3. У знака электроточки: марка (Р — розетка, S — выключатель, Св — светильник, ЭВ — вывод кабеля), ×N — число постов в рамке, гр. — группа щита, Н — высота оси от чистого пола, мм; группы по клавишам выключателя — на листе выключателей.
4. Схема мебели, приборов и декора не является технической документацией для производства мебели; габариты — по паспортам изделий.
5. Картины и зеркала крепить к основанию по паспорту изделия (закладные и анкеры — в перечне скрытых работ); крест — ось центра предмета.

1000 мм · печать 1:1

| Изм. | Кол.уч | Лист | № док. | Подп. | Дата |
|---|---|---|---|---|---|
| Разраб. | | Кырлан А.С. | | | 04.11.26 |
| Пров. | | | | | |
| ГИП | | | | | |
| Н. контр. | | | | | |
| Утв. | | | | | |

**ГД-2026-009-АИ**

Квартира 103 м²

Общая площадь 100,72* м² · * размеры со скана, не замерены (реестр — л. 6, 7, К-1)

Дизайн-проект интерьера

| Стадия | Лист | Листов |
|---|---|---|
| РП | 86 | 120 |

**Развёртка стены В. Гостиная-столовая (пом. 3)**

М 1:25

**Кырлан Александр Сергеевич**


выпуск 04.11.2026 № 35b47f1c2a · стр. 95 из 130

# Развёртка стены Г. Гостиная-столовая (пом. 3)


Гостиная-столовая (пом. 3) · вид изнутри помещения · размеры в мм, отметки в м



## Развёртка стены Г

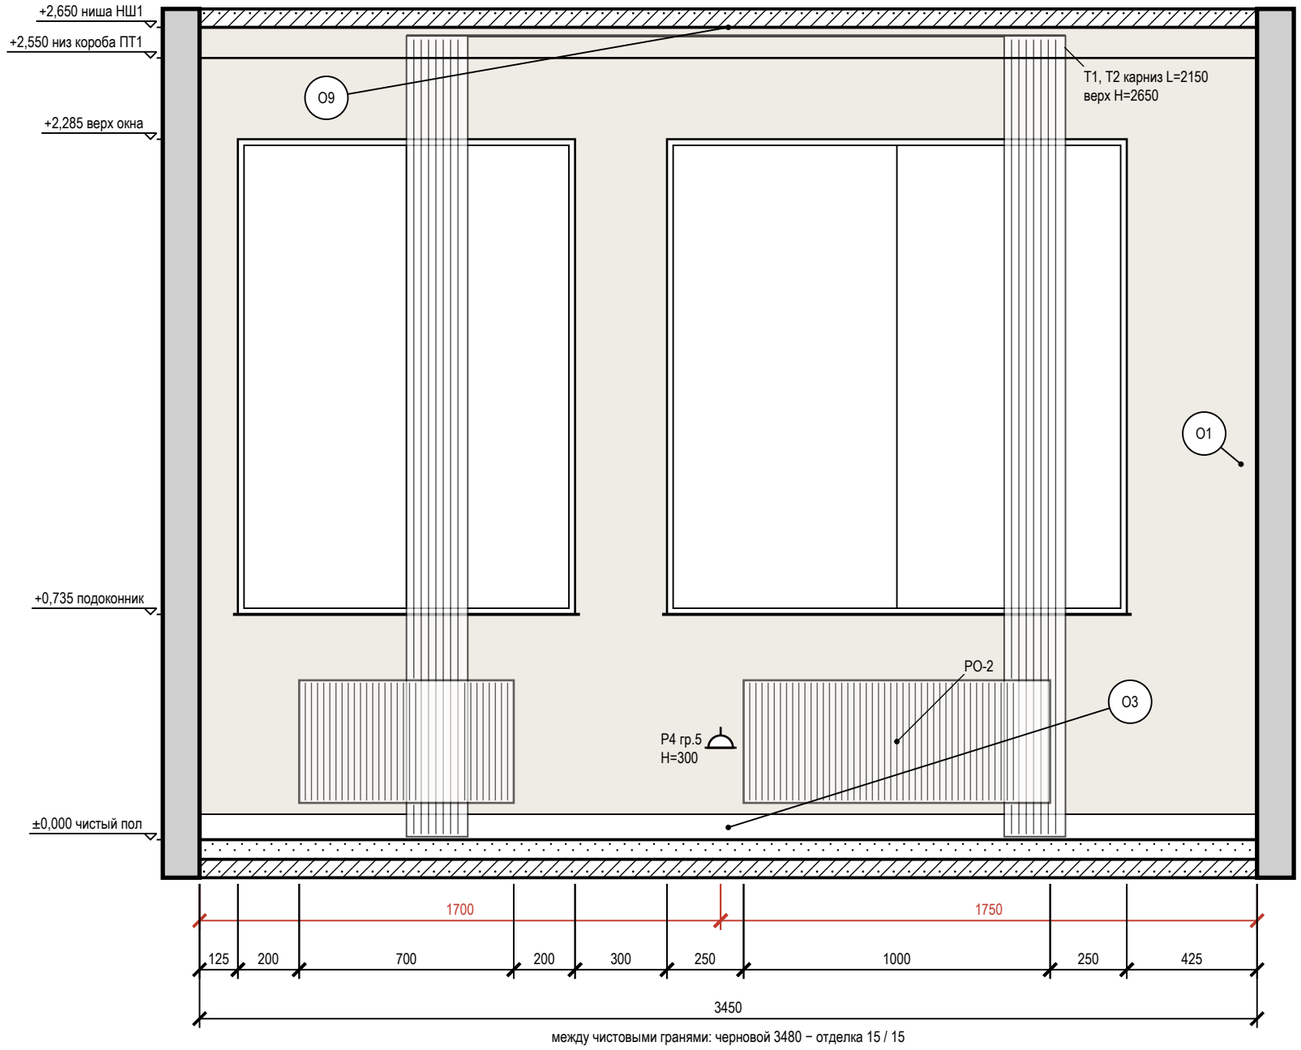


## Схема развёрток (М 1:100)

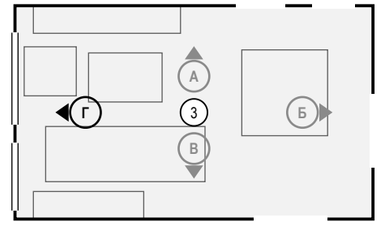


## Условные обозначения

- розетка с заземляющим контактом; у знака — марка, ×N постов в рамке, гр. — группа щита, Н — высота оси, мм
- привязки точек и выводов от угла и от пола, мм
- мебель и приборы — фасад по расстановке (условно)
- карниз (шина) и шторы в собранном виде: марка Т, длина L, верх Н
- окно: проём, рама, подоконник
- радиатор отопления; марка — по плану отопления
- стены и перекрытия в сечении
- окраска: тон — цвет по коду производителя (условно)
- О1 — марка отделки по реестру отделки альбома
- А — марка развёртки: буква стены, стрелка — взгляд

## Ведомость отделки (на листе)

| Марка | Поверхность | Материал, изделие | Цвет, код | Кол. |
|---|---|---|---|---|
| О1 | стены | окраска, Farrow & Ball Modern Emulsion, матовая, подготовка К3 | Farrow & Ball No. 291 «School House White — тёплый меловой белый» | 5,1 м² |
| О3 | плинтус | плинтус МДФ, h 83 мм, Ultrawood Base 5340, ЛДФ под окраску, 83×15 мм, 2440 мм (арт. LDF-BASE-5340), полуглянцевая | Farrow & Ball No. 291 «School House White — тёплый меловой белый» | 3,5 м |
| О9 | потолок | окраска, Farrow & Ball Modern Emulsion, матовая, подготовка Q3 | Farrow & Ball No. 291 «School House White — тёплый меловой белый» | 20,3 м² |

**Допущения и предложения на листе**

Основа листа: размеры сняты со скана обмерного плана KV оформление (см): часть подписей не читается, помещения выровнены по читаемым размерам; контрольный обмер не выполнен (К-1); высота потолка 2650 мм принята по отметкам обмера (Н = 2,50…2,66 м, ригель 2,28 м) — уточнить при обмере (К-2); толщины стен 300 / 120 мм приняты, межквартирная стена и колонны — по скану, не замерены (К-1); разрешённая мощность 15 кВт принята по типовым ТУ; при объединении двух квартир — переоформление ТУ (К-4); подрайон климата не задан — принят не северный (жилые от 2,5 м) (К-8).

Знак «**» — предложение проектировщика, заказчиком не утверждено (согласовать с заказчиком): К-5: дверь пом. 3 (стена Б) — проём в межквартирной стене — объединение квартир, предложение до техзаключения.

См. лист открытых вопросов (лист 6, записи К-1, К-2, К-4, К-5, К-8).

## Примечания

1. Развёртки — вид на стену изнутри помещения, по часовой стрелке; расположение — на схеме листа и на листе 79; размеры — в мм по чистовым поверхностям; отметки — в м от ±0,000; высоты Н — от чистого пола помещения до оси изделия, у декора — до центра.
2. Красная цепочка — привязки электроточек и выводов по осям от угла чистовых стен; высота Н — у знака, от чистого пола до оси; высоты мебели, проёмов и границ отделки — колонкой отметок слева. Стена с 5 и более точками или с мелкими звеньями привязок показана двумя видами: архитектурная развёртка (мебель, отделка, проёмы, высоты) и вид «Привязки» на отдельном листе — точки и выводы с марками, одна цепочка по осям и таблица привязок (каждая точка — строка).
3. У знака электроточки: марка (Р — розетка, S — выключатель, Св — светильник, ЭВ — вывод кабеля), ×N — число постов в рамке, гр. — группа щита, Н — высота оси от чистого пола, мм; группы по клавишам выключателя — на листе выключателей.
4. Схема мебели, приборов и декора не является технической документацией для производства мебели; габариты — по паспортам изделий.
5. Карнизы (шины) — по ведомости текстиля декоратора: длина L и верх Н на развёртке — те же числа, что в ведомости; крепление — до окраски потолка.
6. Линии узора (швы плитки, складки штор, рёбра радиаторов) прерываются у знаков и выносок — просвет между линиями не менее 0,7 мм.

1000 мм · печать 1:1

| Изм. | Кол.уч | Лист | № док. | Подп. | Дата |
|---|---|---|---|---|---|
| Разраб. | | Кырлан А.С. | | | 04.11.26 |
| Пров. | | | | | |
| ГИП | | | | | |
| Н. контр. | | | | | |
| Утв. | | | | | |

**ГД-2026-009-АИ**

Квартира 103 м²

Общая площадь 100,72* м² · * размеры со скана, не замерены (реестр — л. 6, 7, К-1)

Дизайн-проект интерьера

| Стадия | Лист | Листов |
|---|---|---|
| РП | 87 | 120 |

**Развёртка стены Г. Гостиная-столовая (пом. 3)**

М 1:20

**Кырлан Александр Сергеевич**


выпуск 04.11.2026 № 35b47f1c2a · стр. 96 из 130

# Развёртка стены А. Прихожая-холл (пом. 4)

Прихожая-холл (пом. 4) · вид изнутри помещения · размеры в мм, отметки в м


**ПРЕДВАРИТЕЛЬНО · не для производства работ · открыто пунктов: 8 (реестр — л. 6, 7)**

## Развёртка стены А

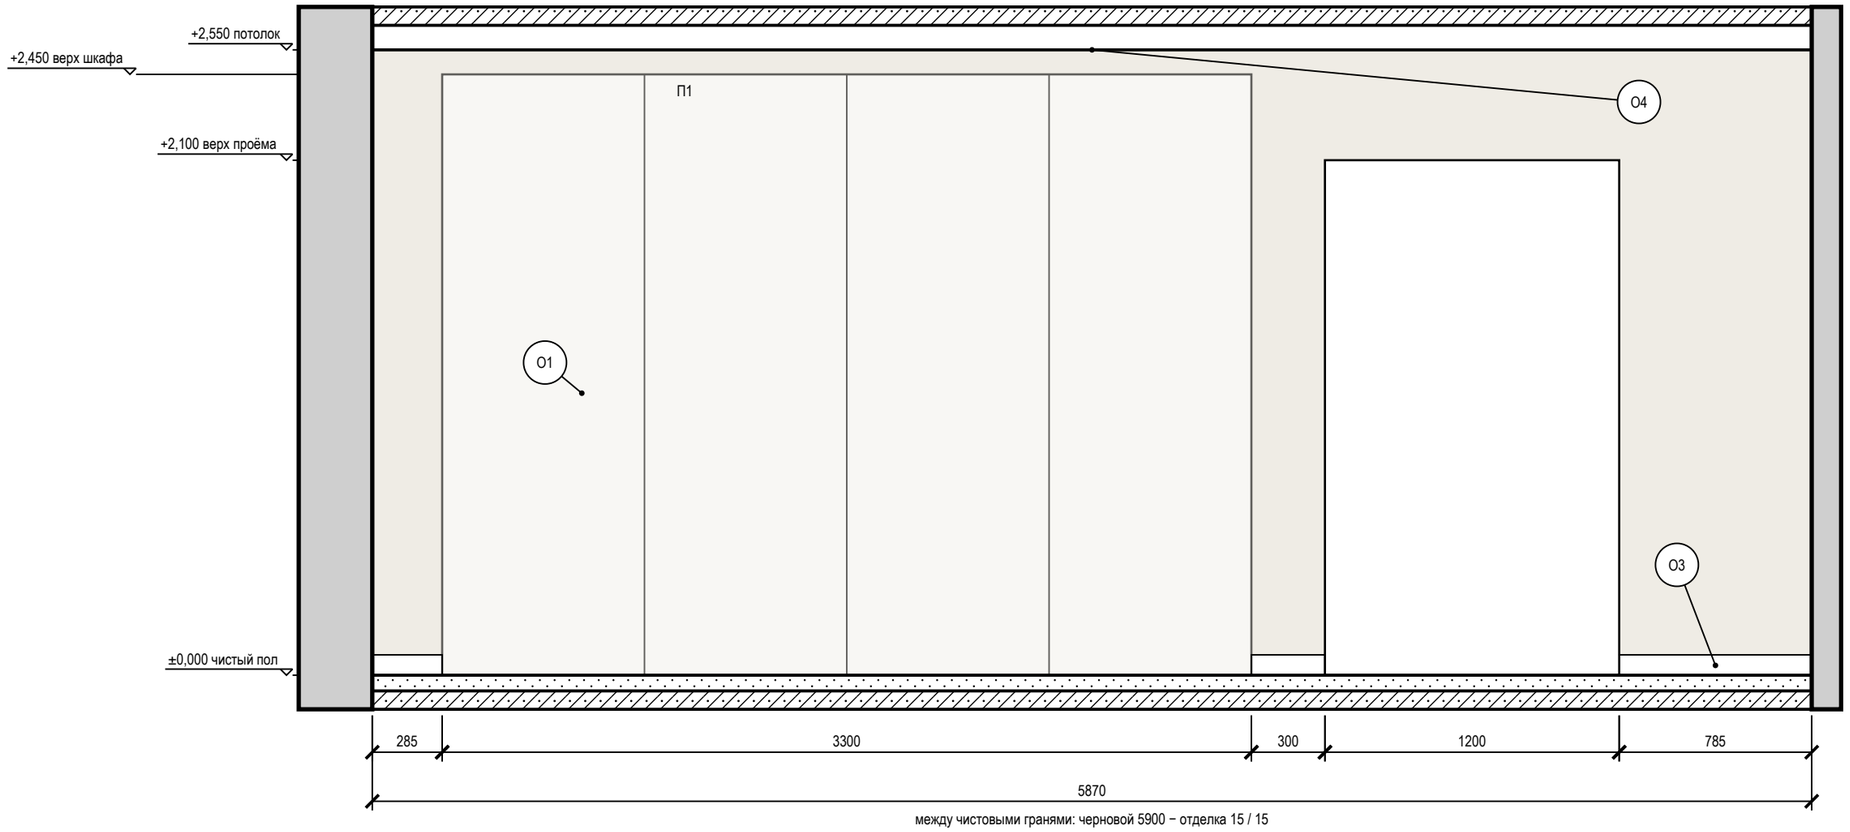


между чистовыми гранями: черновой 5900 − отделка 15 / 15

## Схема развёрток (М 1:100)

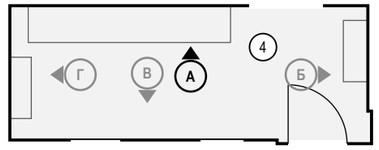


## Условные обозначения

- мебель и приборы — фасад по расстановке (условно)
- дверной проём; марка двери — в кружке
- стены и перекрытия в сечении
- окраска: тон — цвет по коду производителя (условно)
- О1 — марка отделки по реестру отделки альбома
- А — марка развёртки: буква стены, стрелка — взгляд

## Ведомость отделки (на листе)

| Марка | Поверхность | Материал, изделие | Цвет, код | Кол. |
|---|---|---|---|---|
| О1 | стены | окраска, Farrow & Ball Modern Emulsion, матовая, подготовка Q3 | Farrow & Ball No. 291 «School House White тёплый меловой белый» | 12,4 м² |
| О3 | плинтус | плинтус МДФ, h 83 мм, Ultrawood Base 5340, ЛДФ под окраску, 83×15 мм, 2440 мм (арт. LDF-BASE-5340) | Farrow & Ball No. 291 «School House White тёплый меловой белый» | 1,4 м |
| О4 | потолок | окраска, Tikkurila Anti-Reflex 2, глубокоматовая, подготовка Q3 | NCS S 0502-Y «Белый с лёгкой желтизной» | 12,9 м² |

## Примечания

1. Развёртки — вид на стену изнутри помещения, по часовой стрелке; расположение — на схеме листа и на листе 79; размеры — в мм по чистовым поверхностям; отметки — в м от ±0,000; высоты Н — от чистого пола помещения до оси изделия, у декора — до центра.
2. Схема мебели, приборов и декора не является технической документацией для производства мебели; габариты — по паспортам изделий.

**Допущения и предложения на листе**

Основа листа: размеры сняты со скана обмерного плана KV оформление (см): часть подписей не читается, помещения выровнены по читаемым размерам; контрольный обмер не выполнен (К-1); высота потолка 2650 мм принята по отметкам обмера (Н = 2,50…2,66 м, ригель 2,28 м) — уточнить при обмере (К-2); толщины стен 300 / 120 мм приняты, межквартирная стена и колонны — по скану, не замерены (К-1); разрешённая мощность 15 кВт принята по типовым ТУ; при объединении двух квартир — переоформление ТУ (К-4); подрайон климата не задан — принят не северный (жилые от 2,5 м) (К-8).
См. лист открытых вопросов (лист 6, записи К-1, К-2, К-4, К-8).

1000 мм · печать 1:1

| Изм. | Кол.уч | Лист | № док. | Подп. | Дата |
|---|---|---|---|---|---|
| Разраб. | | Кырлан А.С. | | | 04.11.26 |
| Пров. | | | | | |
| ГИП | | | | | |
| | | | | | |
| Н. контр. | | | | | |
| Утв. | | | | | |

**ГД-2026-009-АИ**

Квартира 103 м²

Общая площадь 100,72* м² · * размеры со скана, не замерены (реестр — л. 6, 7, К-1)

Дизайн-проект интерьера

| Стадия | Лист | Листов |
|---|---|---|
| РП | 88 | 120 |

**Развёртка стены А. Прихожая-холл (пом. 4)**

М 1:25

**Кырлан Александр Сергеевич**


выпуск 04.11.2026 № 35b47f1c2a · стр. 97 из 130

# Развёртка стены Б. Прихожая-холл (пом. 4)

Прихожая-холл (пом. 4) · вид изнутри помещения · размеры в мм, отметки в м


ПРЕДВАРИТЕЛЬНО · не для производства работ · открыто пунктов: 8 (реестр — л. 6, 7)

## Развёртка стены Б

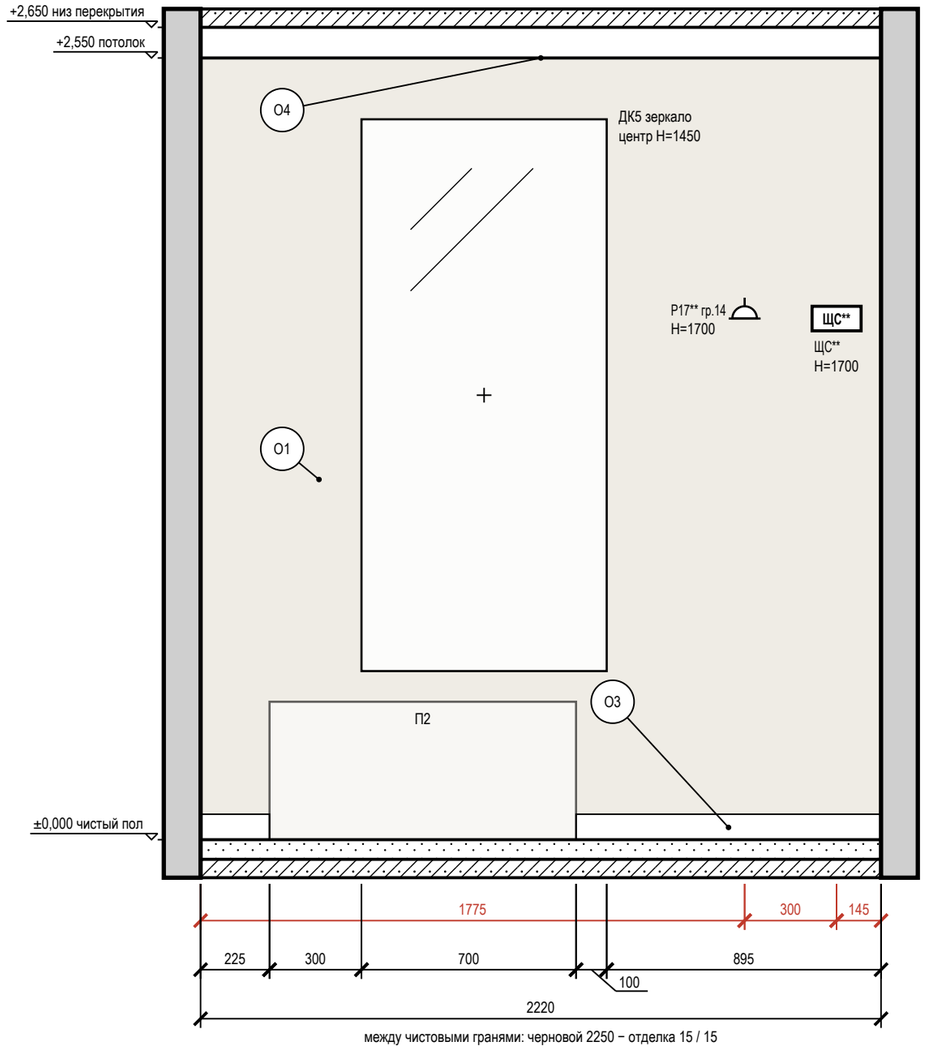


между чистовыми гранями: черновой 2250 − отделка 15 / 15

## Схема развёрток (М 1:100)

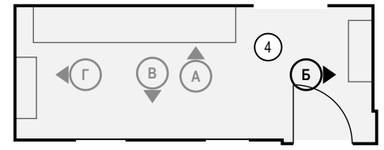


## Условные обозначения

- розетка с заземляющим контактом; у знака — марка, ×N постов в рамке, гр. — группа щита, Н — высота оси, мм
- ЩК — щит квартирный
- привязки точек и выводов от угла и от пола, мм
- мебель и приборы — фасад по расстановке (условно)
- зеркало: марка Д, крест — центр, Н — высота центра, мм
- стены и перекрытия в сечении
- окраска: тон — цвет по коду производителя (условно)
- О1 — марка отделки по реестру отделки альбома
- А — марка развёртки: буква стены, стрелка — взгляд

## Ведомость отделки (на листе)

| Марка | Поверхность | Материал, изделие | Цвет, код | Кол. |
|---|---|---|---|---|
| О1 | стены | окраска, Farrow & Ball Modern Emulsion, матовая, подготовка Q3 | Farrow & Ball No. 291 «School House White — тёплый меловой белый» | 5,7 м² |
| О3 | плинтус | плинтус МДФ, h 83 мм, Ultrawood Base 5340, ЛДФ под окраску, 83×15 мм, 2440 мм (арт. LDF-BASE-5340) | Farrow & Ball No. 291 «School House White — тёплый меловой белый» | 1,2 м |
| О4 | потолок | окраска, Tikkurila Anti-Reflex 2, глубокоматовая, подготовка Q3 | NCS S 0502-Y «Белый с лёгкой желтизной» | 12,9 м² |

**Допущения и предложения на листе**

Основа листа: размеры сняты со скана обмерного плана KV оформление (см): часть подписей не читается, помещения выровнены по читаемым размерам; контрольный обмер не выполнен (К-1); высота потолка 2650 мм принята по отметкам обмера (Н = 2,50…2,66 м, ригель 2,28 м) — уточнить при обмере (К-2); толщины стен 300 / 120 мм приняты, межквартирная стена и колонны — по скану, не замерены (К-1); разрешённая мощность 15 кВт принята по типовым ТУ; при объединении двух квартир — переоформление ТУ (К-4); подрайон климата не задан — принят не северный (жилые от 2,5 м) (К-8).

Знак «**» — предложение проектировщика, заказчиком не утверждено (согласовать с заказчиком): Р17 — высота 1700 мм выше нормы 1 м (ПУЭ 6.6.30) по назначению: питание слаботочного щита ЩС, рядом со щитом на его высоте; ЩС — щит слаботочный: место и состав.

См. лист открытых вопросов (лист 6, записи К-1, К-2, К-4, К-8).

## Примечания

1. Развёртки — вид на стену изнутри помещения, по часовой стрелке; расположение — на схеме листа и на листе 79; размеры — в мм по чистовым поверхностям; отметки — в м от ±0,000; высоты Н — от чистого пола помещения до оси изделия, у декора — до центра.
2. Красная цепочка — привязки электроточек и выводов по осям от угла чистовых стен; высота Н — у знака, от чистого пола до оси; высоты мебели, проёмов и границ отделки — колонкой отметок слева. Стена с 5 и более точками или с мелкими звеньями привязок показана двумя видами: архитектурная развёртка (мебель, отделка, проёмы, высоты) и вид «Привязки» на отдельном листе — точки и выводы с марками, одна цепочка по осям и таблица привязок (каждая точка — строка).
3. У знака электроточки: марка (Р — розетка, S — выключатель, Св — светильник, ЭВ — вывод кабеля), ×N — число постов в рамке, гр. — группа щита, Н — высота оси от чистого пола, мм; группы по клавишам выключателя — на листе выключателей.
4. Схема мебели, приборов и декора не является технической документацией для производства мебели; габариты — по паспортам изделий.
5. Картины и зеркала крепить к основанию по паспорту изделия (закладные и анкеры — в перечне скрытых работ); крест — ось центра предмета.

1000 мм · печать 1:1

| Изм. | Кол.уч | Лист | № док. | Подп. | Дата |
|---|---|---|---|---|---|
| Разраб. | | Кырлан А.С. | | | 04.11.26 |
| Пров. | | | | | |
| ГИП | | | | | |
| | | | | | |
| Н. контр. | | | | | |
| Утв. | | | | | |

**ГД-2026-009-АИ**

Квартира 103 м²

Общая площадь 100,72* м² · * размеры со скана, не замерены (реестр — л. 6, 7, К-1)

Дизайн-проект интерьера

| Стадия | Лист | Листов |
|---|---|---|
| РП | 89 | 120 |

**Развёртка стены Б. Прихожая-холл (пом. 4)**

М 1:20

**Кырлан Александр Сергеевич**


выпуск 04.11.2026 № 35b47f1c2a · стр. 98 из 130

# Развёртка стены В. Прихожая-холл (пом. 4)

Прихожая-холл (пом. 4) · вид изнутри помещения · размеры в мм, отметки в м

**ПРЕДВАРИТЕЛЬНО · не для производства работ · открыто пунктов: 8 (реестр — л. 6, 7)**

## Развёртка стены В

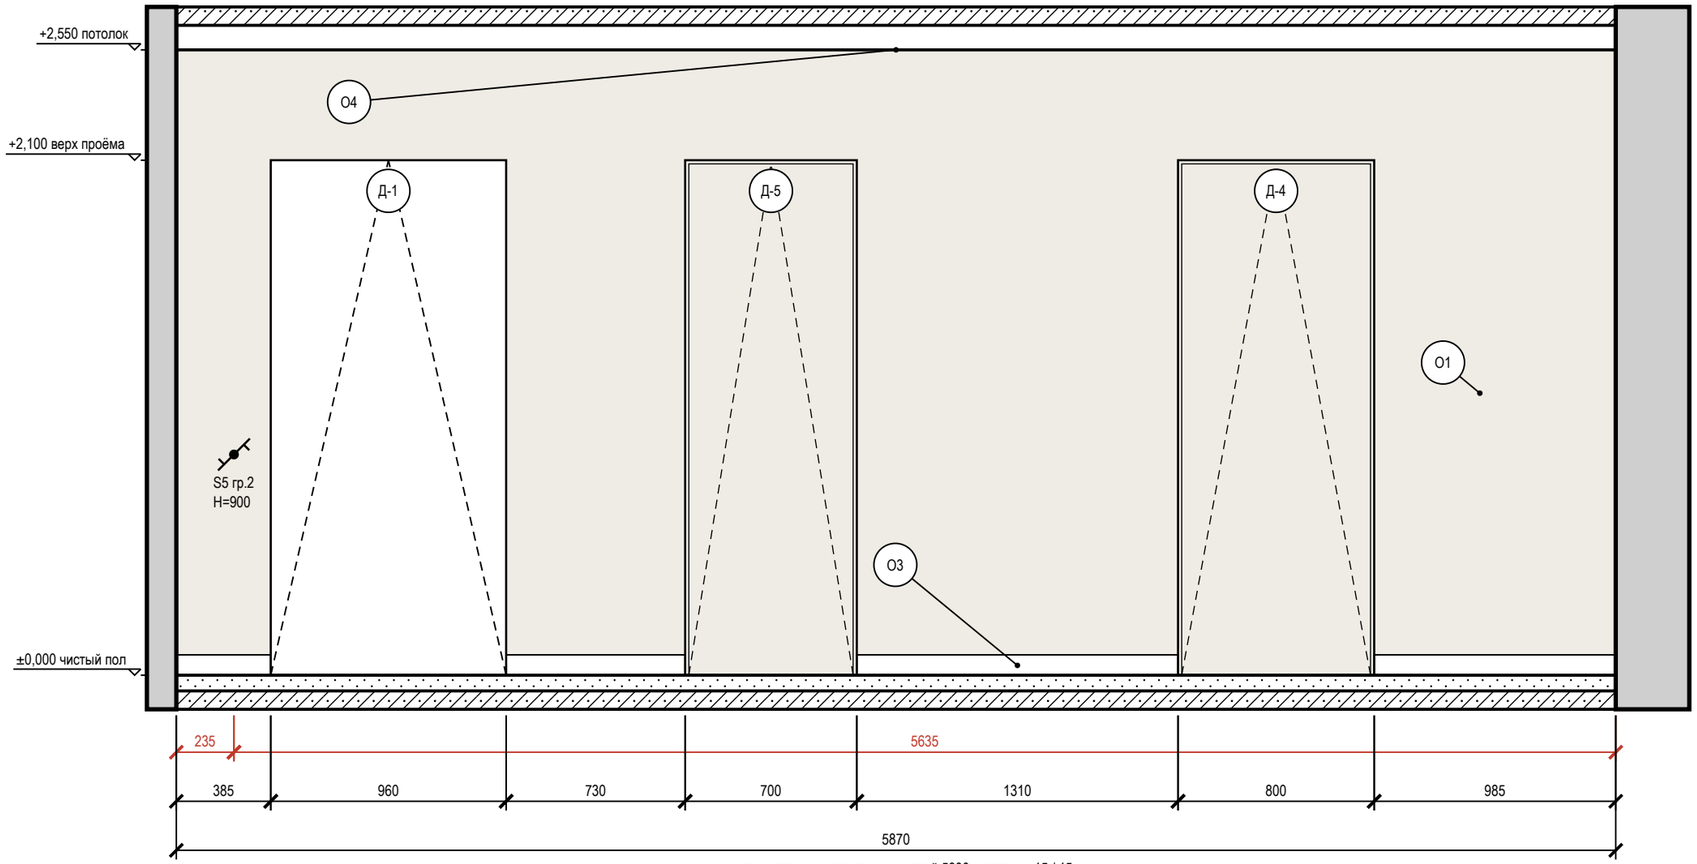



между чистовыми гранями: черновой 5900 − отделка 15 / 15

## Условные обозначения

- выключатель одноклавишный
- выключатель с проходной или перекрёстной клавишей (обратный флажок); тип клавиши — в подписи
- привязки точек и выводов от угла и от пола, мм
- мебель и приборы — фасад по расстановке (условно)
- дверь скрытого монтажа: полотно в плоскости стены (узел — на листе узлов)
- дверной проём; марка двери — в кружке
- стены и перекрытия в сечении
- окраска: тон — цвет по коду производителя (условно)
- О1 — марка отделки по реестру отделки альбома
- А — марка развёртки: буква стены, стрелка — взгляд

## Схема развёрток (М 1:100)

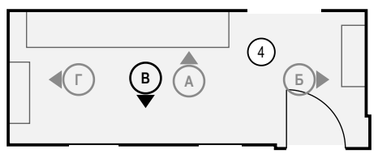


## Ведомость отделки (на листе)

| Марка | Поверхность | Материал, изделие | Цвет, код | Кол. |
|---|---|---|---|---|
| О1 | стены | окраска, Farrow & Ball Modern Emulsion, матовая, подготовка Q3 | Farrow & Ball No. 291 «School House White тёплый меловой белый» | 9,8 м² |
| О3 | плинтус | плинтус МДФ, h 83 мм, Ultrawood Base 5340, ЛДФ под окраску, 83×15 мм, 2440 мм (арт. LDF-BASE-5340) | Farrow & Ball No. 291 «School House White тёплый меловой белый» | 3,4 м |
| О4 | потолок | окраска, Tikkurila Anti-Reflex 2, глубокоматовая, подготовка Q3 | NCS S 0502-Y «Белый с лёгкой желтизной» | 12,9 м² |

**Допущения и предложения на листе**

Основа листа: размеры сняты со скана обмерного плана KV оформление (см): часть подписей не читается, помещения выровнены по читаемым размерам; контрольный обмер не выполнен (К-1); высота потолка 2650 мм принята по отметкам обмера (Н = 2,50…2,66 м, ригель 2,28 м) — уточнить при обмере (К-2); толщины стен 300 / 120 мм приняты, межквартирная стена и колонны — по скану, не замерены (К-1); разрешённая мощность 15 кВт принята по типовым ТУ; при объединении двух квартир — переоформление ТУ (К-4); подрайон климата не задан — принят не северный (жилые от 2,5 м) (К-8).
См. лист открытых вопросов (лист 6, записи К-1, К-2, К-4, К-8).

## Примечания

1. Развёртки — вид на стену изнутри помещения, по часовой стрелке; расположение — на схеме листа и на листе 79; размеры — в мм по чистовым поверхностям; отметки — в м от ±0,000; высоты Н — от чистого пола помещения до оси изделия, у декора — до центра.
2. Красная цепочка — привязки электроточек и выводов по осям от угла чистовых стен; высота Н — у знака, от чистого пола до оси; высоты мебели, проёмов и границ отделки — колонкой отметок слева. Стена с 5 и более точками или с мелкими звеньями привязок показана двумя видами: архитектурная развёртка (мебель, отделка, проёмы, высоты) и вид «Привязки» на отдельном листе — точки и выводы с марками, одна цепочка по осям и таблица привязок (каждая точка — строка).
3. У знака электроточки: марка (Р — розетка, S — выключатель, Св — светильник, ЭВ — вывод кабеля), ×N — число постов в рамке, гр. — группа щита, Н — высота оси от чистого пола, мм; группы по клавишам выключателя — на листе выключателей.
4. Схема мебели, приборов и декора не является технической документацией для производства мебели; габариты — по паспортам изделий.
5. Двери скрытого монтажа — полотно в плоскости стены, отделка стены по полотну, плинтус прерывается у короба (узел — на листе узлов).

1000 мм · печать 1:1

| Изм. | Кол.уч | Лист | № док. | Подп. | Дата |
|---|---|---|---|---|---|
| Разраб. | | Кырлан А.С. | | | 04.11.26 |
| Пров. | | | | | |
| ГИП | | | | | |
| Н. контр. | | | | | |
| Утв. | | | | | |

**ГД-2026-009-АИ**

Квартира 103 м²

Общая площадь 100,72* м² · * размеры со скана, не замерены (реестр — л. 6, 7, К-1)

Дизайн-проект интерьера

| Стадия | Лист | Листов |
|---|---|---|
| РП | 90 | 120 |

**Развёртка стены В. Прихожая-холл (пом. 4)**

М 1:25

**Кырлан Александр Сергеевич**


выпуск 04.11.2026 № 35b47f1c2a · стр. 99 из 130

# Развёртка стены Г. Прихожая-холл (пом. 4)

Прихожая-холл (пом. 4) · вид изнутри помещения · размеры в мм, отметки в м


ПРЕДВАРИТЕЛЬНО · не для производства работ · открыто пунктов: 8 (реестр — л. 6, 7)

**Развёртка стены Г**

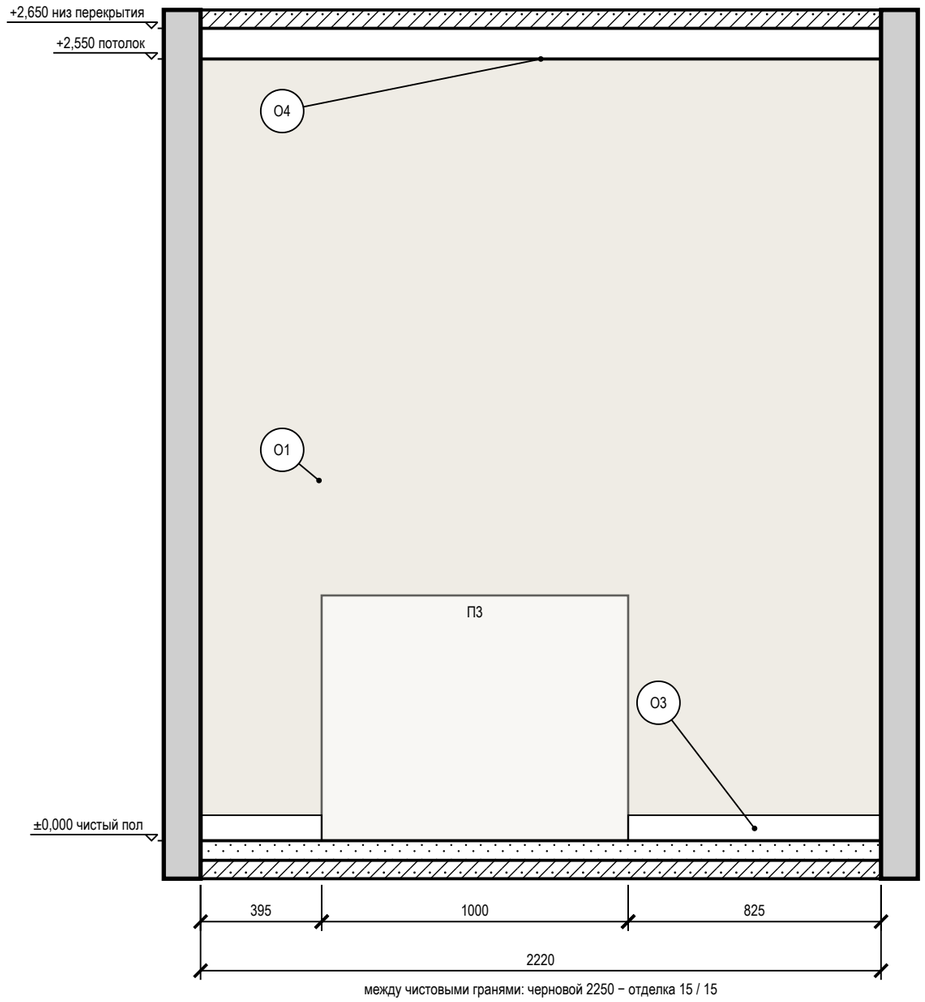


между чистовыми гранями: черновой 2250 − отделка 15 / 15

## Схема развёрток (М 1:100)

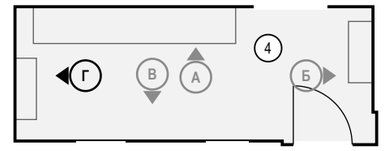


## Условные обозначения

- мебель и приборы — фасад по расстановке (условно)
- стены и перекрытия в сечении
- окраска: тон — цвет по коду производителя (условно)
- О1 — марка отделки по реестру отделки альбома
- А — марка развёртки: буква стены, стрелка — взгляд

## Ведомость отделки (на листе)

| Марка | Поверхность | Материал, изделие | Цвет, код | Кол. |
|---|---|---|---|---|
| О1 | стены | окраска, Farrow & Ball Modern Emulsion, матовая, подготовка Q3 | Farrow & Ball No. 291 «School House White — тёплый меловой белый» | 5,7 м² |
| О3 | плинтус | плинтус МДФ, h 83 мм, Ultrawood Base 5340, ЛДФ под окраску, 83×15 мм, 2440 мм (арт. LDF-BASE-5340) | Farrow & Ball No. 291 «School House White — тёплый меловой белый» | 1,2 м |
| О4 | потолок | окраска, Tikkurila Anti-Reflex 2, глубокоматовая, подготовка Q3 | NCS S 0502-Y «Белый с лёгкой желтизной» | 12,9 м² |

## Примечания

1. Развёртки — вид на стену изнутри помещения, по часовой стрелке; расположение — на схеме листа и на листе 79; размеры — в мм по чистовым поверхностям; отметки — в м от ±0,000; высоты Н — от чистого пола помещения до оси изделия, у декора — до центра.
2. Схема мебели, приборов и декора не является технической документацией для производства мебели; габариты — по паспортам изделий.

**Допущения и предложения на листе**

Основа листа: размеры сняты со скана обмерного плана KV оформление (см): часть подписей не читается, помещения выровнены по читаемым размерам; контрольный обмер не выполнен (К-1); высота потолка 2650 мм принята по отметкам обмера (Н = 2,50…2,66 м, ригель 2,28 м) — уточнить при обмере (К-2); толщины стен 300 / 120 мм приняты, межквартирная стена и колонны — по скану, не замерены (К-1); разрешённая мощность 15 кВт принята по типовым ТУ; при объединении двух квартир — переоформление ТУ (К-4); подрайон климата не задан — принят не северный (жилые от 2,5 м) (К-8).
См. лист открытых вопросов (лист 6, записи К-1, К-2, К-4, К-8).

1000 мм · печать 1:1

| Изм. | Кол.уч | Лист | № док. | Подп. | Дата |
|---|---|---|---|---|---|
| Разраб. | | Кырлан А.С. | | | 04.11.26 |
| Пров. | | | | | |
| ГИП | | | | | |
| | | | | | |
| Н. контр. | | | | | |
| Утв. | | | | | |

**ГД-2026-009-АИ**

Квартира 103 м²

Общая площадь 100,72* м² · * размеры со скана, не замерены (реестр — л. 6, 7, К-1)

Дизайн-проект интерьера

| Стадия | Лист | Листов |
|---|---|---|
| РП | 91 | 120 |

**Развёртка стены Г. Прихожая-холл (пом. 4)**

М 1:20

**Кырлан Александр Сергеевич**


выпуск 04.11.2026 № 35b47f1c2a · стр. 100 из 130

# Развёртки стен Б, В. Кухня (пом. 5), кухонный фронт

Кухня (пом. 5) · вид изнутри помещения · размеры в мм, отметки в м


**ПРЕДВАРИТЕЛЬНО · не для производства работ · открыто пунктов: 8 (реестр — л. 6, 7)**

## Развёртка стены Б

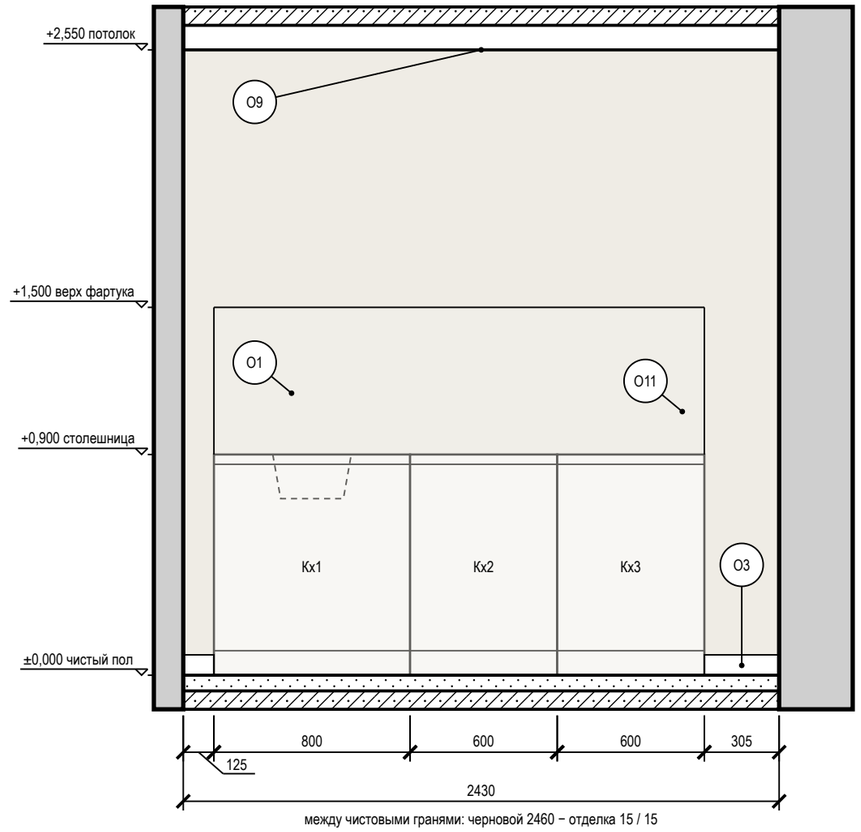



между чистовыми гранями: черновой 2460 − отделка 15 / 15

## Развёртка стены В

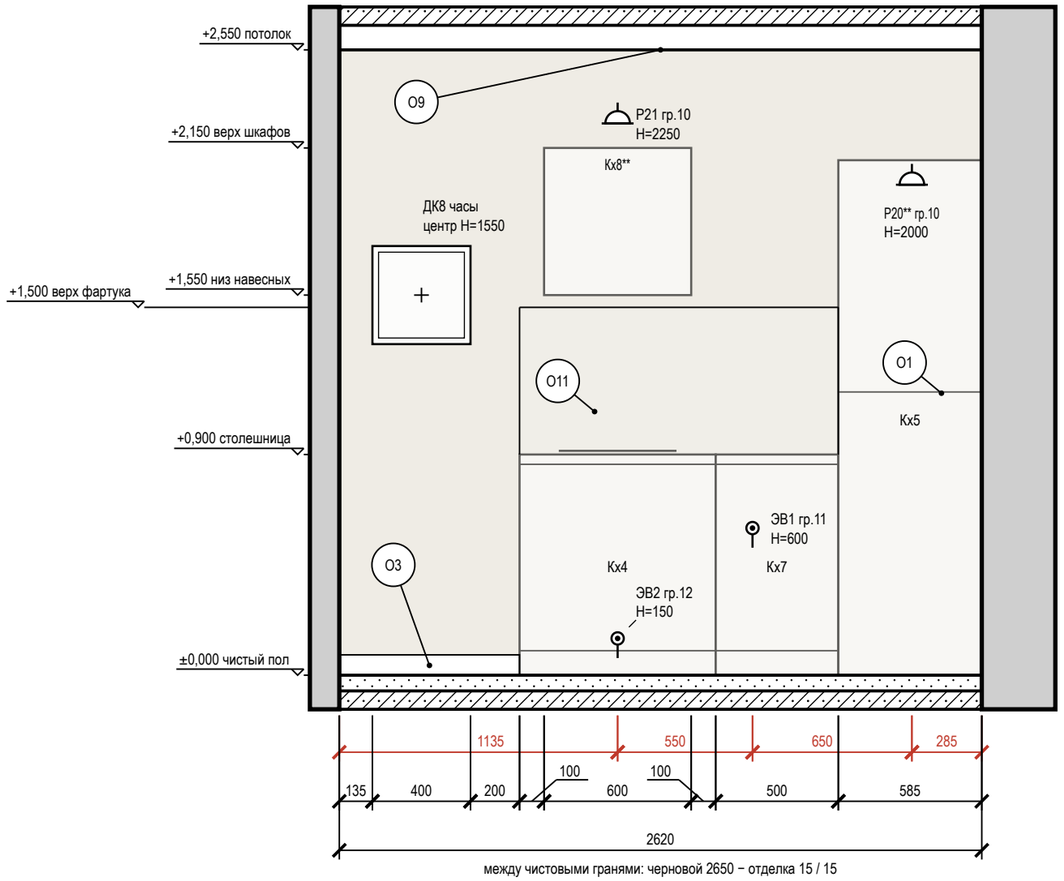


между чистовыми гранями: черновой 2650 − отделка 15 / 15

## Схема развёрток (М 1:100)

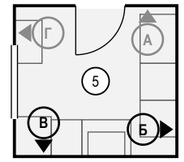


## Условные обозначения

- розетка с заземляющим контактом; у знака — марка, ×N постов в рамке, гр. — группа щита, Н — высота оси, мм
- вывод кабеля для подключения прибора (без розетки), марка ЭВ
- привязки точек и выводов от угла и от пола, мм
- мебель и приборы — фасад по расстановке (условно)
- картина (декор): марка Д, крест — центр, Н — высота центра, мм
- стены и перекрытия в сечении
- плитка: сетка швов по формату, ▲ — ось старта
- окраска: тон — цвет по коду производителя (условно)
- О1 — марка отделки по реестру отделки альбома
- А — марка развёртки: буква стены, стрелка — взгляд

**Допущения и предложения на листе**

Основа листа: размеры сняты со скана обмерного плана KV оформление (см): часть подписей не читается, помещения выровнены по читаемым размерам; контрольный обмер не выполнен (К-1); высота потолка 2650 мм принята по отметкам обмера (Н = 2,50…2,66 м, ригель 2,28 м) — уточнить при обмере (К-2); толщины стен 300 / 120 мм приняты, межквартирная стена и колонны — по скану, не замерены (К-1); разрешённая мощность 15 кВт принята по типовым ТУ; при объединении двух квартир — переоформление ТУ (К-4); подрайон климата не задан — принят не северный (жилые от 2,5 м) (К-8).

Знак «**» — предложение проектировщика, заказчиком не утверждено (согласовать с заказчиком): Кх8 — над индукционной панелью Кх4 нужна вытяжка: в составе кухни её не было, розетка вытяжки образца висела без потребителя; Р20 — высота 2000 мм выше нормы 1 м (ПУЭ 6.6.30) по назначению: розетка встроенного прибора — в колонне Кх5 над нишей, в антресоли за съёмной панелью.

См. лист открытых вопросов (лист 6, записи К-1, К-2, К-4, К-8).

## Примечания

1. Развёртки — вид на стену изнутри помещения, по часовой стрелке; расположение — на схеме листа и на листе 79; размеры — в мм по чистовым поверхностям; отметки — в м от ±0,000; высоты Н — от чистого пола помещения до оси изделия, у декора — до центра.
2. Красная цепочка — привязки электроточек и выводов по осям от угла чистовых стен; высота Н — у знака, от чистого пола до оси; высоты мебели, проёмов и границ отделки — колонкой отметок слева. Стена с 5 и более точками или с мелкими звеньями привязок показана двумя видами: архитектурная развёртка (мебель, отделка, проёмы, высоты) и вид «Привязки» на отдельном листе — точки и выводы с марками, одна цепочка по осям и таблица привязок (каждая точка — строка).
3. Стена Б показана двумя видами: здесь — архитектурная развёртка (мебель, отделка, проёмы, высоты), электроточки и выводы ВК с привязками и таблицей — на листе 93 («Привязки»).
4. У знака электроточки: марка (Р — розетка, S — выключатель, Св — светильник, ЭВ — вывод кабеля), ×N — число постов в рамке, гр. — группа щита, Н — высота оси от чистого пола, мм; группы по клавишам выключателя — на листе выключателей.
5. Схема мебели, приборов и декора не является технической документацией для производства мебели; габариты — по паспортам изделий.
6. Картины и зеркала крепить к основанию по паспорту изделия (закладные и анкеры — в перечне скрытых работ); крест — ось центра предмета.
7. Выводы кухонной техники — по утверждённому проекту кухни: привязки выводов даются от осей модулей гарнитура.

1000 мм · печать 1:1

| Изм. | Кол.уч | Лист | № док. | Подп. | Дата |
|---|---|---|---|---|---|
| Разраб. | | Кырлан А.С. | | | 04.11.26 |
| Пров. | | | | | |
| ГИП | | | | | |
| | | | | | |
| Н. контр. | | | | | |
| Утв. | | | | | |

**ГД-2026-009-АИ**

Квартира 103 м²

Общая площадь 100,72* м² · * размеры со скана, не замерены (реестр — л. 6, 7, К-1)

Дизайн-проект интерьера

| Стадия | Лист | Листов |
|---|---|---|
| РП | 92 | 120 |

**Развёртки стен Б, В. Кухня (пом. 5), кухонный фронт**

М 1:25

**Кырлан Александр Сергеевич**


выпуск 04.11.2026 № 35b47f1c2a · стр. 101 из 130

# Привязки электроточек и выводов ВК, стена Б. Кухня (пом. 5)

Кухня (пом. 5) · вид изнутри помещения · привязки в мм, отметки в м · к развёртке на листе 92

ПРЕДВАРИТЕЛЬНО · не для производства работ · открыто пунктов: 8 (реестр — л. 6, 7)

## Развёртка стены Б: электроточки и выводы

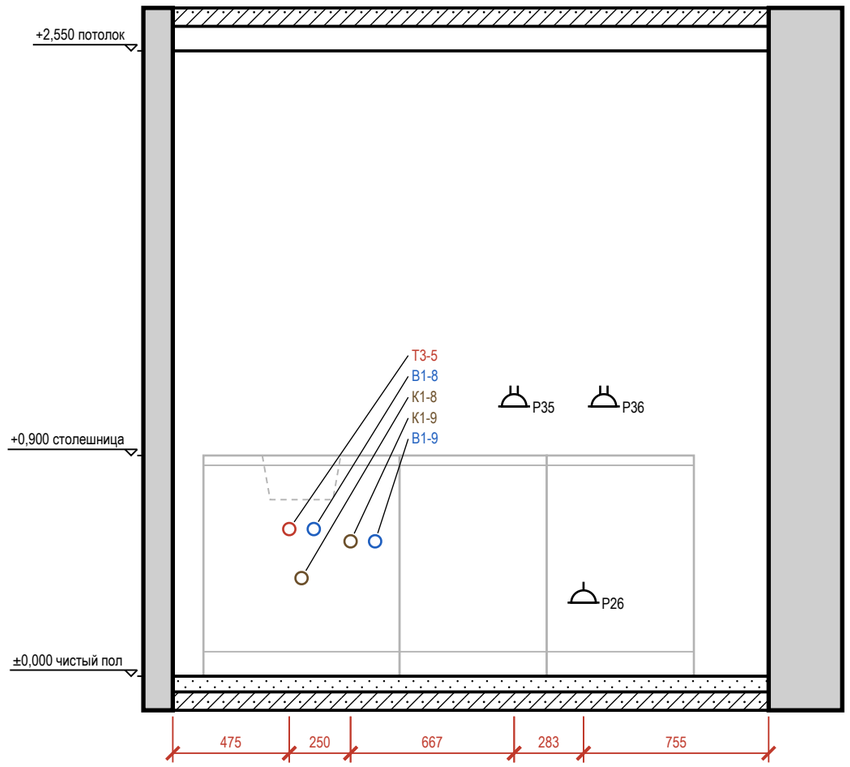



## Таблица привязок электроточек и выводов

| Марка | Назначение | От угла, мм | Н от пола, мм | Примечание |
|---|---|---|---|---|
| Т3-5 | горячая вода — мойка кухонная | 475 | 600* | межос. 100 |
| К1-8 | канализация — мойка кухонная | 525 | 400* | Ø50 |
| В1-8 | холодная вода — мойка кухонная | 575 | 600* | межос. 100 |
| К1-9 | канализация — посудомоечная машина | 725 | 550* | Ø40; слив ПММ в шкафу мойки |
| В1-9 | холодная вода — посудомоечная машина | 825 | 550* | кран ПММ в шкафу мойки |
| Р35 | розетка: фартук | 1392 | 1100 | рамка 2 поста, гр. 9 |
| Р26 | розетка: посудомоечная машина — в соседнем модуле, за ящиком | 1675 | 300 | гр. 13 |
| Р36 | розетка: фартук | 1758 | 1100 | рамка 2 поста, гр. 9 |

## Условные обозначения

- розетка с заземляющим контактом; у знака — марка, ×N постов в рамке, гр. — группа щита, Н — высота оси, мм
- вывод В1 (код — в ведомости привязок)
- вывод Т3 (код — в ведомости привязок)
- вывод К1 (код — в ведомости привязок)
- привязки точек и выводов от угла и от пола, мм
- марка развёртки: буква стены, стрелка — взгляд

## Схема развёрток (М 1:100)

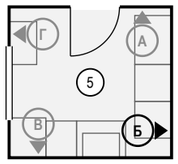


## Примечания

1. Вид «Привязки» стены Б — электроточки и выводы ВК; архитектурная развёртка (мебель, отделка, проёмы, высоты) — на листе 92, расположение — на листе 79. Мебель и приборы — подложкой для ориентира; их марки и обозначения мебели, проёмов и стен — там же.
2. Привязки — в мм: по горизонтали от левого чистового угла стены до оси изделия, Н — от чистого пола до оси; все точки — в таблице привязок. Красная цепочка — привязки по осям; точки ближе 150 мм одна к другой в цепочку не дробятся — их привязки только в таблице.
3. У знака — марка электроточки (Р — розетка, S — выключатель, Св — светильник, ЭВ — вывод кабеля); посты в рамке и группа щита — в графе «Примечание»; группы по клавишам выключателя — на листе выключателей.
4. Коды выводов ВК: В1 — холодная вода, Т3 — горячая вода, К1 — канализация; номер после дефиса — номер вывода на листе выводов сантехники; * — высота принята по типовой практике монтажа, окончательно — по паспорту прибора.
5. Выводы кухонной техники — по утверждённому проекту кухни: привязки выводов даются от осей модулей гарнитура.

**Допущения и предложения на листе**

Основа листа: размеры сняты со скана обмерного плана KV оформление (см): часть подписей не читается, помещения выровнены по читаемым размерам; контрольный обмер не выполнен (К-1); высота потолка 2650 мм принята по отметкам обмера (Н = 2,50…2,66 м, ригель 2,28 м) — уточнить при обмере (К-2); толщины стен 300 / 120 мм приняты, межквартирная стена и колонны — по скану, не замерены (К-1); разрешённая мощность 15 кВт принята по типовым ТУ; при объединении двух квартир — переоформление ТУ (К-4); подрайон климата не задан — принят не северный (жилые от 2,5 м) (К-8).

См. лист открытых вопросов (лист 6, записи К-1, К-2, К-4, К-8).

1000 мм · печать 1:1

| Изм. | Кол.уч | Лист | № док. | Подп. | Дата |
|---|---|---|---|---|---|
| Разраб. | | Кырлан А.С. | | | 04.11.26 |
| Пров. | | | | | |
| ГИП | | | | | |
| | | | | | |
| Н. контр. | | | | | |
| Утв. | | | | | |

**ГД-2026-009-АИ**

Квартира 103 м²

Общая площадь 100,72* м² · * размеры со скана, не замерены (реестр — л. 6, 7, К-1)

Дизайн-проект интерьера

| Стадия | Лист | Листов |
|---|---|---|
| РП | 93 | 120 |

**Привязки электроточек и выводов ВК, стена Б. Кухня (пом. 5)**

М 1:25

**Кырлан Александр Сергеевич**


выпуск 04.11.2026 № 35b47f1c2a · стр. 102 из 130

# Развёртки стен А, Г. Кухня (пом. 5)

Кухня (пом. 5) · вид изнутри помещения · размеры в мм, отметки в м


**ПРЕДВАРИТЕЛЬНО · не для производства работ · открыто пунктов: 8 (реестр — л. 6, 7)**

## Развёртка стены А

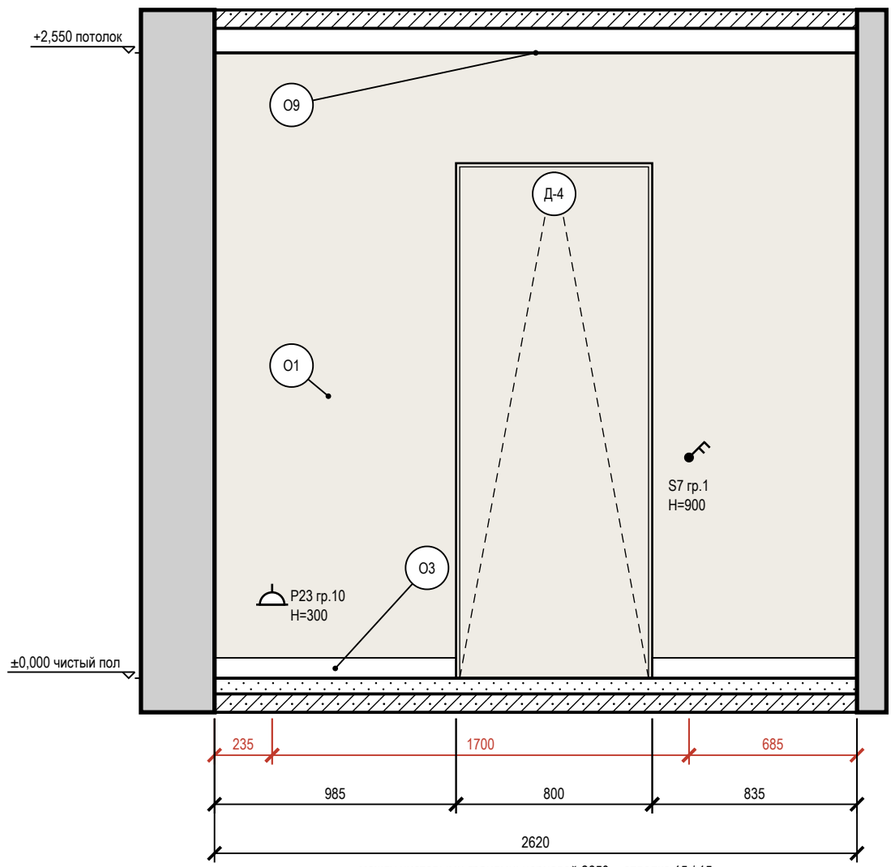



между чистовыми гранями: черновой 2650 − отделка 15 / 15

## Развёртка стены Г

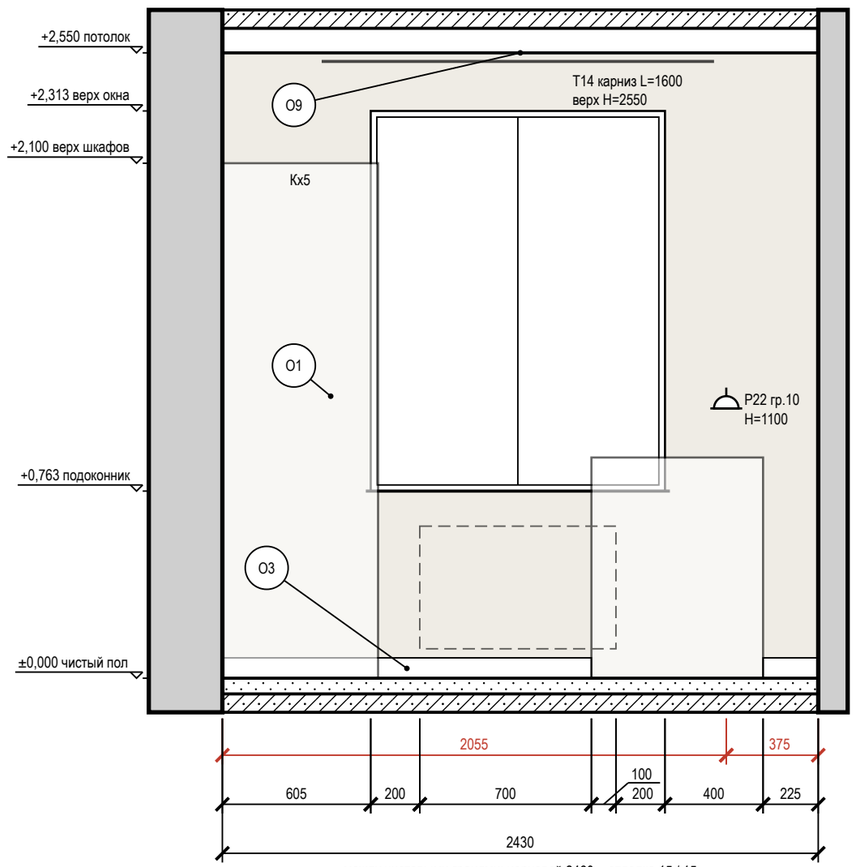


между чистовыми гранями: черновой 2460 − отделка 15 / 15

## Схема развёрток (М 1:100)

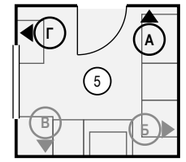


## Условные обозначения

- розетка с заземляющим контактом; у знака — марка, ×N постов в рамке, гр. — группа щита, H — высота оси, мм
- выключатель одноклавишный
- выключатель двухклавишный (флажков — по числу клавиш)
- привязки точек и выводов от угла и от пола, мм
- мебель и приборы — фасад по расстановке (условно)
- карниз (шина) и шторы в собранном виде: марка T, длина L, верх H
- дверь скрытого монтажа: полотно в плоскости стены (узел — на листе узлов)
- окно: проём, рама, подоконник
- радиатор отопления; марка — по плану отопления
- стены и перекрытия в сечении
- окраска: тон — цвет по коду производителя (условно)
- О1 — марка отделки по реестру отделки альбома
- А — марка развёртки: буква стены, стрелка — взгляд

**Допущения и предложения на листе**

Основа листа: размеры сняты со скана обмерного плана KV оформление (см): часть подписей не читается, помещения выровнены по читаемым размерам; контрольный обмер не выполнен (К-1); высота потолка 2650 мм принята по отметкам обмера (H = 2,50…2,66 м, ригель 2,28 м) — уточнить при обмере (К-2); толщины стен 300 / 120 мм приняты, межквартирная стена и колонны — по скану, не замерены (К-1); разрешённая мощность 15 кВт принята по типовым ТУ; при объединении двух квартир — переоформление ТУ (К-4); подрайон климата не задан — принят не северный (жилые от 2,5 м) (К-8).

См. лист открытых вопросов (лист 6, записи К-1, К-2, К-4, К-8).

## Примечания

1. Развёртки — вид на стену изнутри помещения, по часовой стрелке; расположение — на схеме листа и на листе 79; размеры — в мм по чистовым поверхностям; отметки — в м от ±0,000; высоты H — от чистого пола помещения до оси изделия, у декора — до центра.
2. Красная цепочка — привязки электроточек и выводов по осям от угла чистовых стен; высота H — у знака, от чистого пола до оси; высоты мебели, проёмов и границ отделки — колонкой отметок слева. Стена с 5 и более точками или с мелкими звеньями привязок показана двумя видами: архитектурная развёртка (мебель, отделка, проёмы, высоты) и вид «Привязки» на отдельном листе — точки и выводы с марками, одна цепочка по осям и таблица привязок (каждая точка — строка).
3. У знака электроточки: марка (Р — розетка, S — выключатель, Св — светильник, ЭВ — вывод кабеля), ×N — число постов в рамке, гр. — группа щита, H — высота оси от чистого пола, мм; группы по клавишам выключателя — на листе выключателей.
4. Схема мебели, приборов и декора не является технической документацией для производства мебели; габариты — по паспортам изделий.
5. Карнизы (шины) — по ведомости текстиля декоратора: длина L и верх H на развёртке — те же числа, что в ведомости; крепление — до окраски потолка.
6. Двери скрытого монтажа — полотно в плоскости стены, отделка стены по полотну, плинтус прерывается у короба (узел — на листе узлов).

1000 мм · печать 1:1

| Изм. | Кол.уч | Лист | № док. | Подп. | Дата |
|---|---|---|---|---|---|
| Разраб. | | Кырлан А.С. | | | 04.11.26 |
| Пров. | | | | | |
| ГИП | | | | | |
| | | | | | |
| Н. контр. | | | | | |
| Утв. | | | | | |

**ГД-2026-009-АИ**

Квартира 103 м²

Общая площадь 100,72* м² · * размеры со скана, не замерены (реестр — л. 6, 7, К-1)

Дизайн-проект интерьера

| Стадия | Лист | Листов |
|---|---|---|
| РП | 94 | 120 |

**Развёртки стен А, Г. Кухня (пом. 5)**

М 1:25

**Кырлан Александр Сергеевич**


выпуск 04.11.2026 № 35b47f1c2a · стр. 103 из 130

# Развёртки стен А, Б, В. Ванная (пом. 6)

Ванная (пом. 6) · вид изнутри помещения · размеры в мм, отметки в м


**ПРЕДВАРИТЕЛЬНО · не для производства работ · открыто пунктов: 8 (реестр — л. 6, 7)**

## Развёртка стены А

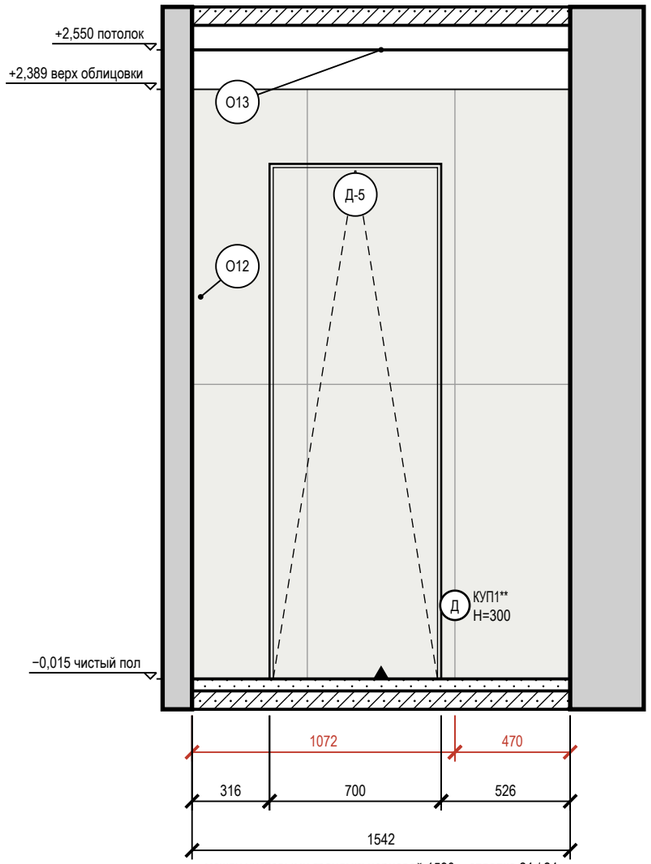



между чистовыми гранями: черновой 1590 − отделка 24 / 24

## Развёртка стены Б

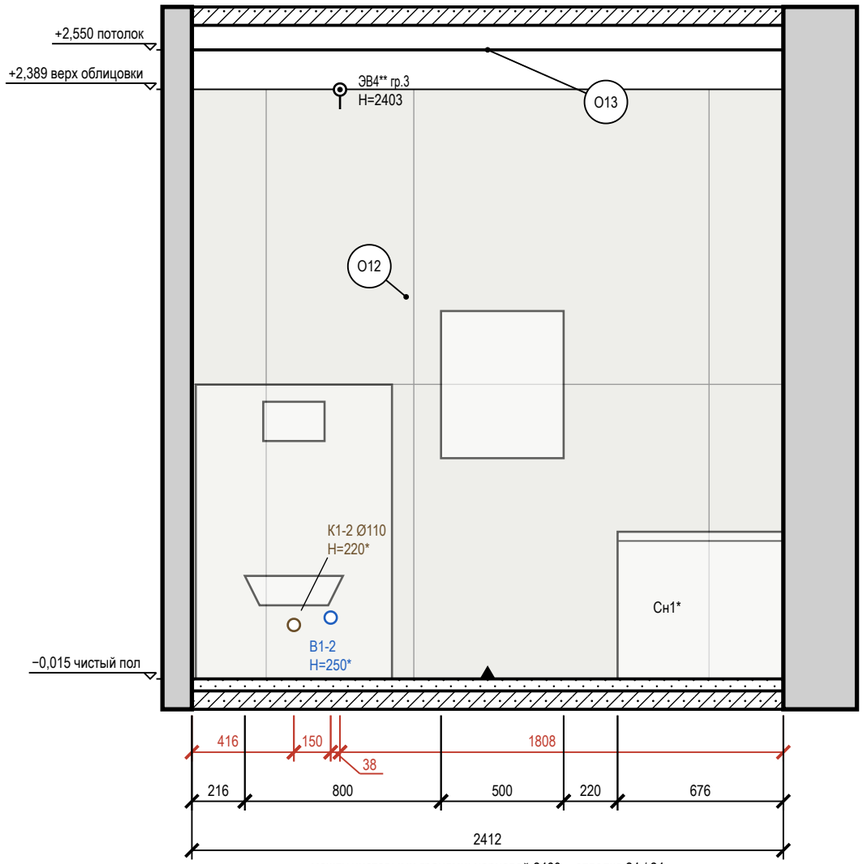



между чистовыми гранями: черновой 2460 − отделка 24 / 24

## Развёртка стены В

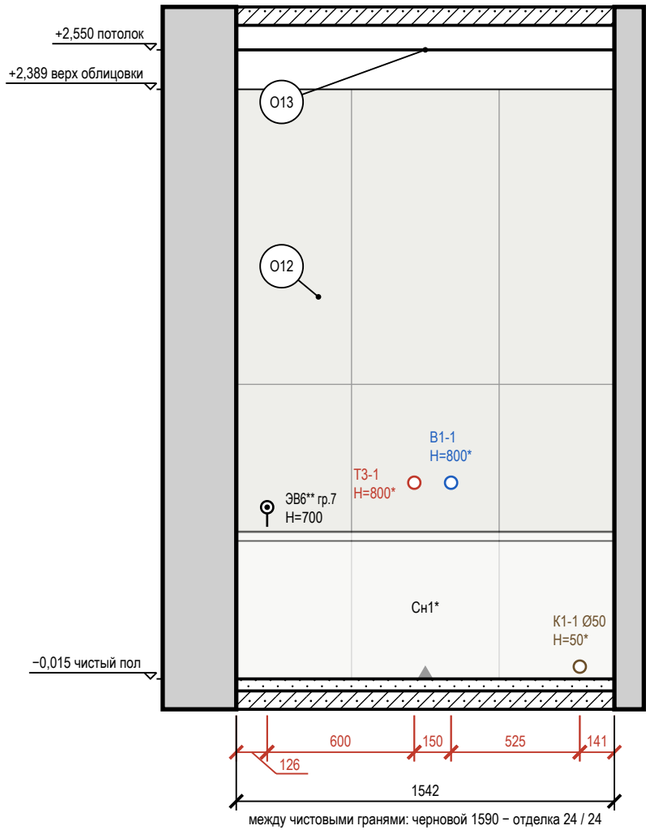


между чистовыми гранями: черновой 1590 − отделка 24 / 24

### Схема развёрток (М 1:100)

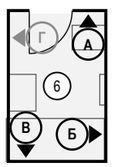


### Условные обозначения

- вывод кабеля для подключения прибора (без розетки), марка ЭВ
- вывод В1 (код — в ведомости привязок)
- вывод Т3 (код — в ведомости привязок)
- вывод К1 (код — в ведомости привязок)
- привязки точек и выводов от угла и от пола, мм
- мебель и приборы — фасад по расстановке (условно)
- дверь скрытого монтажа: полотно в плоскости стены (узел — на листе узлов)
- стены и перекрытия в сечении
- плитка: сетка швов по формату, ▲ — ось старта
- О1 — марка отделки по реестру отделки альбома
- А — марка развёртки: буква стены, стрелка — взгляд

### Ведомость отделки (на листе)

| Марка | Поверхность | Материал, изделие | Цвет, код | Кол. |
|---|---|---|---|---|
| О12 | стены | облицовка плиткой, Atlas Concorde Marvel Travertine, 600×1200×9 мм, A8UZ, затирка CG2WA | Atlas Concorde A8UZ «Marvel Travertine» | 11,7 м² |
| О13 | потолок | окраска, Tikkurila Luja 7, матовая, подготовка Q3 | NCS S 0502-Y «Белый с лёгкой желтизной» | 3,9 м² |

Допущения и предложения на листе. Знак «**» предложено (согласовать). См. лист открытых вопросов (лист 6).

### Примечания

1. Развёртки — вид на стену изнутри помещения, по часовой стрелке; расположение — на схеме листа и на листе 79; размеры — в мм по чистовым поверхностям; отметки — в м от ±0,000; высоты Н — от чистого пола помещения до оси изделия, у декора — до центра.
2. Красная цепочка — привязки электроточек и выводов по осям от угла чистовых стен; высота Н — у знака, от чистого пола до оси; высоты мебели, проёмов и границ отделки — колонкой отметок слева. Стена с 5 и более точками или с мелкими звеньями привязок показана двумя видами: архитектурная развёртка (мебель, отделка, проёмы, высоты) и вид «Привязки» на отдельном листе — точки и выводы с марками, одна цепочка по осям и таблица привязок (каждая точка — строка).
3. У знака электроточки: марка (Р — розетка, S — выключатель, Св — светильник, ЭВ — вывод кабеля), ×N — число постов в рамке, гр. — группа щита, Н — высота оси от чистого пола, мм; группы по клавишам выключателя — на листе выключателей.
4. Схема мебели, приборов и декора не является технической документацией для производства мебели; габариты — по паспортам изделий (* — высота не задана в проекте, показана по типовому изделию).
5. Выводы ВК — коды и высоты по листу выводов сантехники; * — высота принята по типовой практике монтажа, окончательно — по паспорту прибора.
6. Облицовка — по сетке швов 2 мм, раскладка от оси стены (треугольник у пола), целые ряды от пола; подрезки — по листу раскладки плитки.
7. Гидроизоляция в 2 слоя, заход на стены 200 мм; над ванной — до 2000 и 300 мм за борт — до облицовки, с актом скрытых работ и тестом проливом (узел — на листе узлов).
8. Двери скрытого монтажа — полотно в плоскости стены, отделка стены по полотну, плинтус прерывается у короба (узел — на листе узлов).

1000 мм · печать 1:1

| Изм. | Кол.уч | Лист | № док. | Подп. | Дата |
|---|---|---|---|---|---|
| Разраб. | | Кырлан А.С. | | | 04.11.26 |
| Пров. | | | | | |
| ГИП | | | | | |
| Н. контр. | | | | | |
| Утв. | | | | | |

**ГД-2026-009-АИ**

Квартира 103 м²

Общая площадь 100,72* м² · * размеры со скана, не замерены (реестр — л. 6, 7, К-1)

Дизайн-проект интерьера

| Стадия | Лист | Листов |
|---|---|---|
| РП | 95 | 120 |

**Развёртки стен А, Б, В. Ванная (пом. 6)**

М 1:25

**Кырлан Александр Сергеевич**


выпуск 04.11.2026 № 35b47f1c2a · стр. 104 из 130

# Развёртка стены Г. Ванная (пом. 6)

Ванная (пом. 6) · вид изнутри помещения · размеры в мм, отметки в м




**Развёртка стены Г**

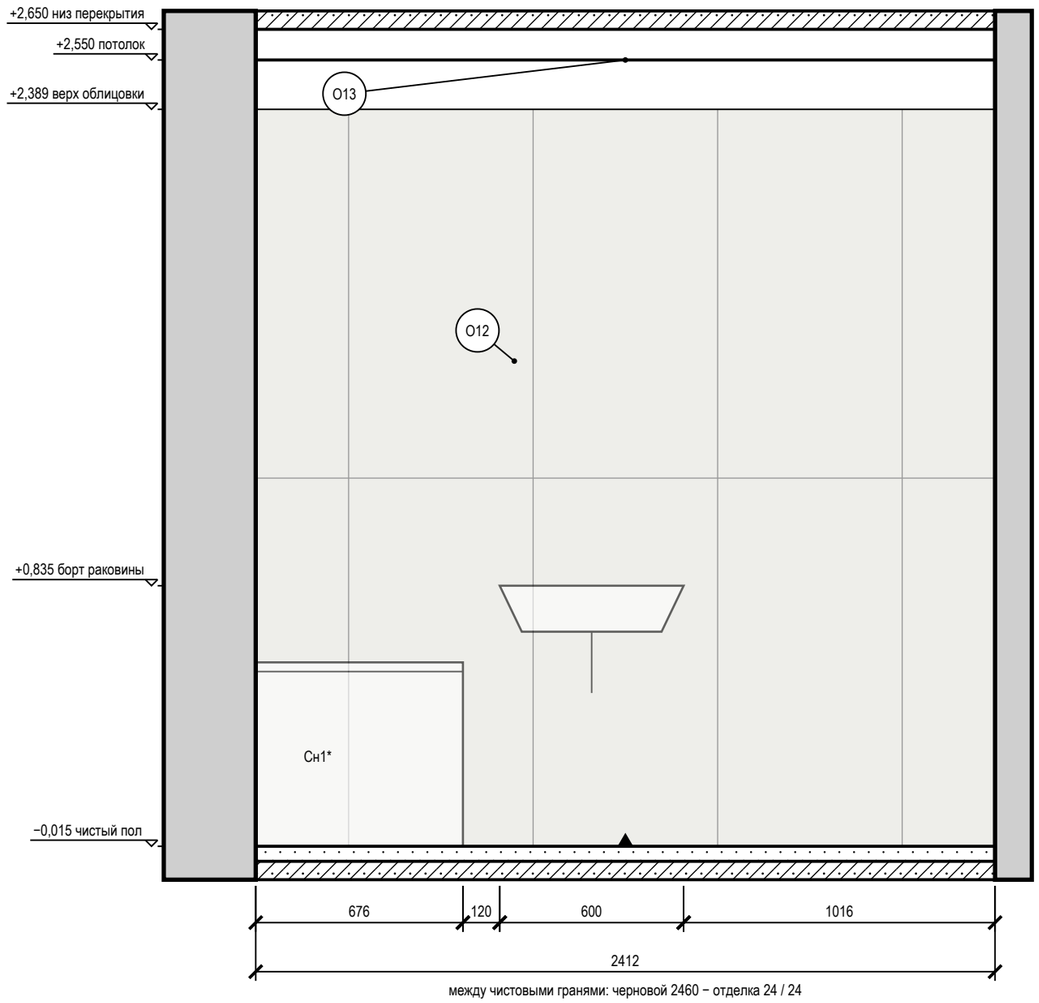


между чистовыми гранями: черновой 2460 − отделка 24 / 24

## Схема развёрток (М 1:100)

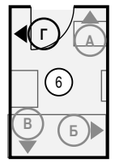


## Условные обозначения

- мебель и приборы — фасад по расстановке (условно)
- стены и перекрытия в сечении
- плитка: сетка швов по формату, ▲ — ось старта
- О1 — марка отделки по реестру отделки альбома
- А — марка развёртки: буква стены, стрелка — взгляд

## Ведомость отделки (на листе)

| Марка | Поверхность | Материал, изделие | Цвет, код | Кол. |
|---|---|---|---|---|
| О12 | стены | облицовка плиткой, Atlas Concorde Marvel Travertine, 600×1200×9 мм, A8UZ, затирка CG2WA | Atlas Concorde A8UZ «Marvel Travertine» | 5,8 м² |
| О13 | потолок | окраска, Tikkurila Luja 7, матовая, подготовка Q3 | NCS S 0502-Y «Белый с лёгкой желтизной» | 3,9 м² |

**Допущения и предложения на листе**

Основа листа: размеры сняты со скана обмерного плана KV оформление (см): часть подписей не читается, помещения выровнены по читаемым размерам; контрольный обмер не выполнен (К-1); высота потолка 2650 мм принята по отметкам обмера (Н = 2,50…2,66 м, ригель 2,28 м) — уточнить при обмере (К-2); толщины стен 300 / 120 мм приняты, межквартирная стена и колонны — по скану, не замерены (К-1); разрешённая мощность 15 кВт принята по типовым ТУ; при объединении двух квартир — переоформление ТУ (К-4); подрайон климата не задан — принят не северный (жилые от 2,5 м) (К-8).

См. лист открытых вопросов (лист 6, записи К-1, К-2, К-4, К-8).

## Примечания

1. Развёртки — вид на стену изнутри помещения, по часовой стрелке; расположение — на схеме листа и на листе 79; размеры — в мм по чистовым поверхностям; отметки — в м от ±0,000; высоты Н — от чистого пола помещения до оси изделия, у декора — до центра.
2. Стена Г показана двумя видами: здесь — архитектурная развёртка (мебель, отделка, проёмы, высоты), электроточки и выводы ВК с привязками и таблицей — на листе 97 («Привязки»).
3. Схема мебели, приборов и декора не является технической документацией для производства мебели; габариты — по паспортам изделий (* — высота не задана в проекте, показана по типовому изделию).
4. Облицовка — по сетке швов 2 мм, раскладка от оси стены (треугольник у пола), целые ряды от пола; подрезки — по листу раскладки плитки.
5. Гидроизоляция в 2 слоя, заход на стены 200 мм; над ванной — до 2000 и 300 мм за борт — до облицовки, с актом скрытых работ и тестом проливом (узел — на листе узлов).

1000 мм · печать 1:1

| Изм. | Кол.уч | Лист | № док. | Подп. | Дата |
|---|---|---|---|---|---|
| Разраб. | | Кырлан А.С. | | | 04.11.26 |
| Пров. | | | | | |
| ГИП | | | | | |
| | | | | | |
| Н. контр. | | | | | |
| Утв. | | | | | |

**ГД-2026-009-АИ**

Квартира 103 м²

Общая площадь 100,72* м² · * размеры со скана, не замерены (реестр — л. 6, 7, К-1)

| Дизайн-проект интерьера | Стадия | Лист | Листов |
|---|---|---|---|
| | РП | 96 | 120 |

**Развёртка стены Г. Ванная (пом. 6)**

М 1:20

**Кырлан Александр Сергеевич**


выпуск 04.11.2026 № 35b47f1c2a · стр. 105 из 130

# Привязки электроточек и выводов ВК, стена Г. Ванная (пом. 6)

Ванная (пом. 6) · вид изнутри помещения · привязки в мм, отметки в м · к развёртке на листе 96

**ПРЕДВАРИТЕЛЬНО · не для производства работ · открыто пунктов: 8 (реестр — л. 6, 7)**

## Развёртка стены Г: электроточки и выводы

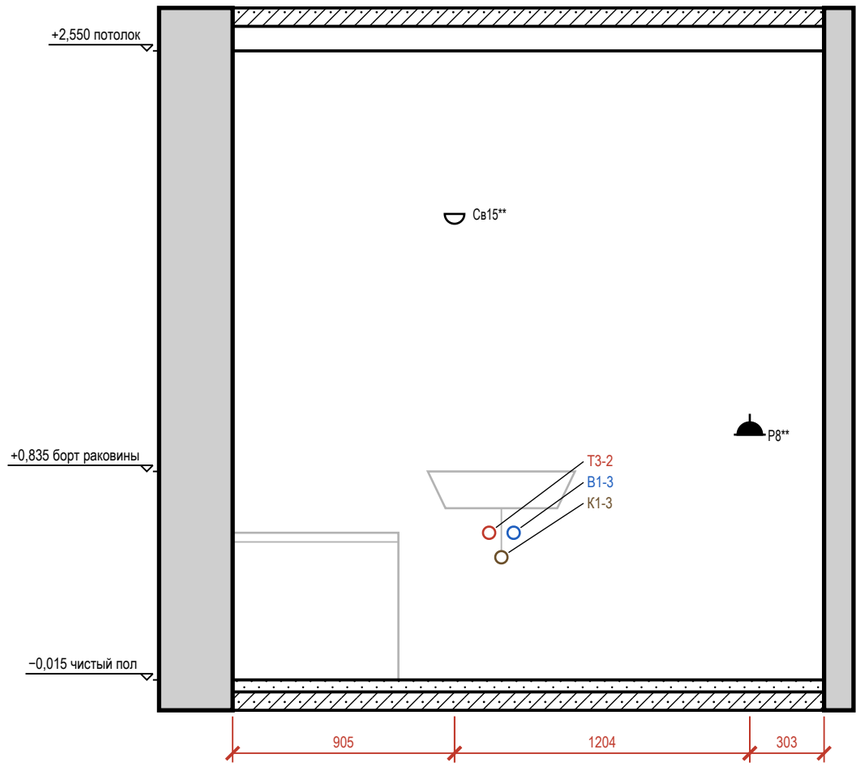



## Таблица привязок электроточек и выводов

| Марка | Назначение | От угла, мм | Н от пола, мм | Примечание |
|---|---|---|---|---|
| Св15** | светильник настенный | 905 | 1900 | гр. 3 |
| Т3-2 | горячая вода — умывальник | 1046 | 600* | межос. 100 |
| К1-3 | канализация — умывальник | 1096 | 500* | Ø50 |
| В1-3 | холодная вода — умывальник | 1146 | 600* | межос. 100 |
| Р8** | розетка: фен у умывальника | 2109 | 1000 | гр. 7, IP44 |

## Условные обозначения

- розетка влагозащищённая IP44
- светильник настенный (бра), Н — высота оси
- вывод В1 (код — в ведомости привязок)
- вывод Т3 (код — в ведомости привязок)
- вывод К1 (код — в ведомости привязок)
- привязки точек и выводов от угла и от пола, мм
- марка развёртки: буква стены, стрелка — взгляд

## Схема развёрток (М 1:50)

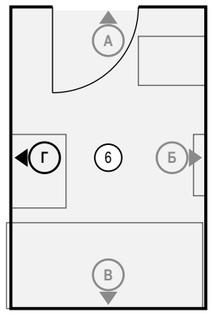


## Примечания

1. Вид «Привязки» стены Г — электроточки и выводы ВК; архитектурная развёртка (мебель, отделка, проёмы, высоты) — на листе 96, расположение — на листе 79. Мебель и приборы — подложкой для ориентира; их марки и обозначения мебели, проёмов и стен — там же.
2. Привязки — в мм: по горизонтали от левого чистового угла стены до оси изделия, Н — от чистого пола до оси; все точки — в таблице привязок. Красная цепочка — привязки по осям; точки ближе 150 мм одна к другой в цепочку не дробятся — их привязки только в таблице.
3. У знака — марка электроточки (Р — розетка, S — выключатель, Св — светильник, ЭВ — вывод кабеля); посты в рамке и группа щита — в графе «Примечание»; группы по клавишам выключателя — на листе выключателей.
4. Коды выводов ВК: В1 — холодная вода, Т3 — горячая вода, К1 — канализация; номер после дефиса — номер вывода на листе выводов сантехники; * — высота принята по типовой практике монтажа, окончательно — по паспорту прибора.

**Допущения и предложения на листе**

Основа листа: размеры сняты со скана обмерного плана KV оформление (см): часть подписей не читается, помещения выровнены по читаемым размерам; контрольный обмер не выполнен (К-1); высота потолка 2650 мм принята по отметкам обмера (Н = 2,50…2,66 м, ригель 2,28 м) — уточнить при обмере (К-2); толщины стен 300 / 120 мм приняты, межквартирная стена и колонны — по скану, не замерены (К-1); разрешённая мощность 15 кВт принята по типовым ТУ; при объединении двух квартир — переоформление ТУ (К-4); подрайон климата не задан — принят не северный (жилые от 2,5 м) (К-8).

Знак «**» — предложение проектировщика, заказчиком не утверждено (согласовать с заказчиком): Св15 — Сдвиг под раскладку плитки стены Г на 141 мм вдоль стены — ось на шве или в центре плитки, привязка по таблице листа; ИЗ-1: Р8 — по образцу: Р7, Р8 и Р33 на высоте 1000 мм — верхний предел нормы (ПУЭ, п. 6.6.30, не выше 1 м); флаг решения снят; сдвиг под раскладку плитки стены Г на 87 мм вдоль стены — ось на шве или в центре плитки, привязка по таблице листа.

См. лист открытых вопросов (лист 6, записи ИЗ-1, К-1, К-2, К-4, К-8).

1000 мм · печать 1:1

| Изм. | Кол.уч | Лист | № док. | Подп. | Дата |
|---|---|---|---|---|---|
| Разраб. | | Кырлан А.С. | | | 04.11.26 |
| Пров. | | | | | |
| ГИП | | | | | |
| Н. контр. | | | | | |
| Утв. | | | | | |

**ГД-2026-009-АИ**

Квартира 103 м²

Общая площадь 100,72* м² · * размеры со скана, не замерены (реестр — л. 6, 7, К-1)

Дизайн-проект интерьера

| Стадия | Лист | Листов |
|---|---|---|
| РП | 97 | 120 |

**Привязки электроточек и выводов ВК, стена Г. Ванная (пом. 6)**

М 1:25

**Кырлан Александр Сергеевич**


выпуск 04.11.2026 № 35b47f1c2a · стр. 106 из 130

# Развёртки стен. Постирочная (пом. 7)

Постирочная (пом. 7) · вид изнутри помещения · размеры в мм, отметки в м


ПРЕДВАРИТЕЛЬНО · не для производства работ · открыто пунктов: 8 (реестр — л. 6, 7)

## Развёртка стены А

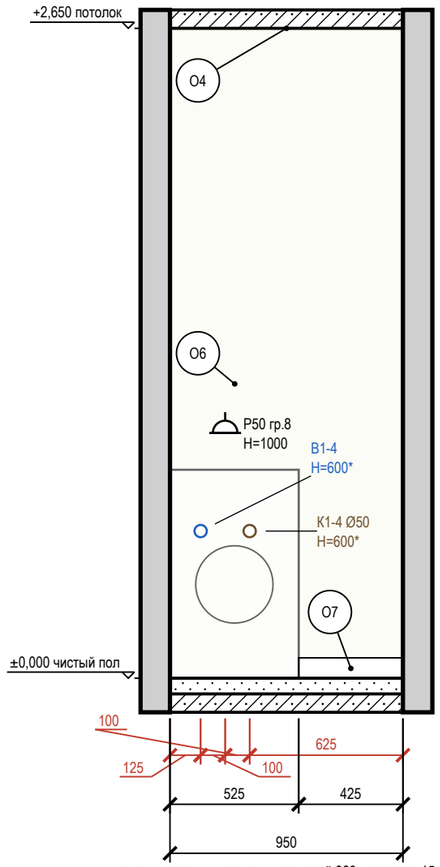



между чистовыми гранями: черновой 980 − отделка 15 / 15

## Развёртка стены Б

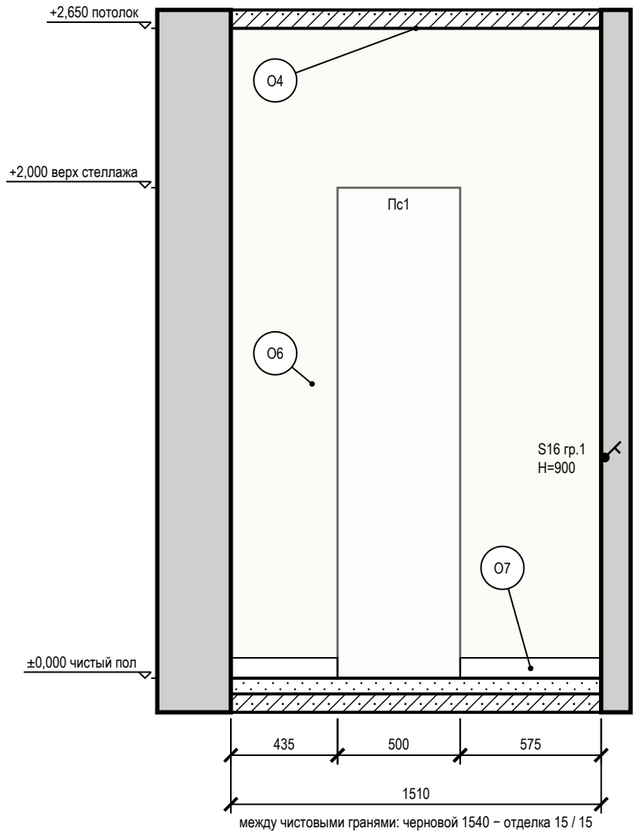



между чистовыми гранями: черновой 1540 − отделка 15 / 15

## Развёртка стены В

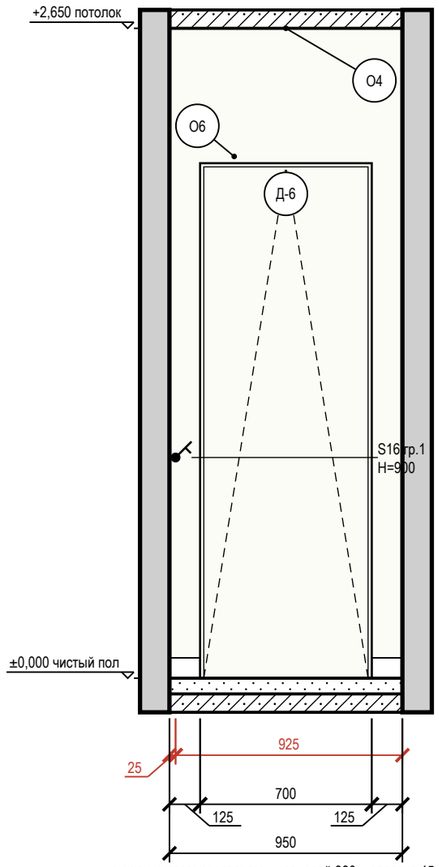



между чистовыми гранями: черновой 980 − отделка 15 / 15

## Развёртка стены Г

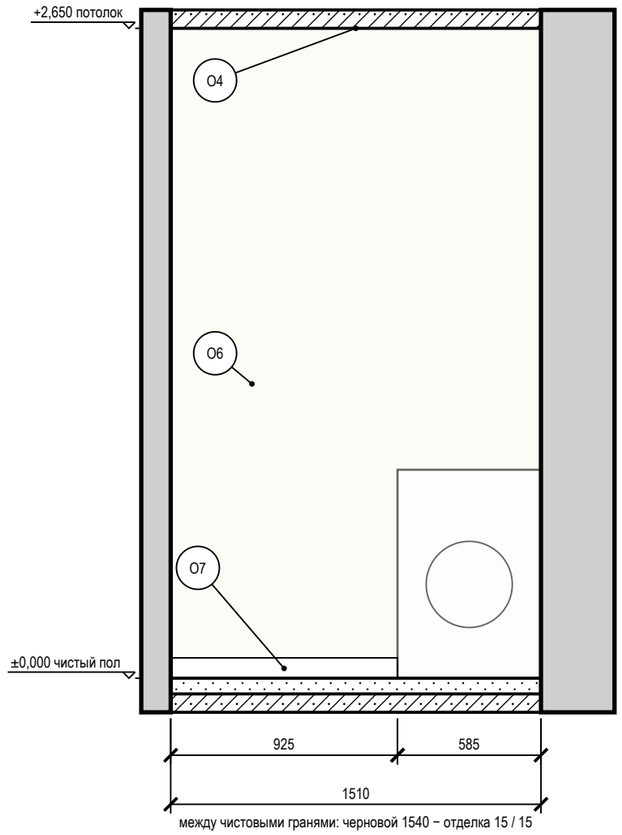


между чистовыми гранями: черновой 1540 − отделка 15 / 15

## Схема развёрток (М 1:100)

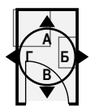


## Условные обозначения

- розетка с заземляющим контактом; у знака — марка, ×N постов в рамке, гр. — группа щита, Н — высота оси, мм
- выключатель одноклавишный
- вывод В1 (код — в ведомости привязок)
- вывод К1 (код — в ведомости привязок)
- привязки точек и выводов от угла и от пола, мм
- мебель и приборы — фасад по расстановке (условно)
- дверь скрытого монтажа: полотно в плоскости стены (узел — на листе узлов)
- стены и перекрытия в сечении
- окраска: тон — цвет по коду производителя (условно)
- О1 — марка отделки по реестру отделки альбома
- А — марка развёртки: буква стены, стрелка — взгляд

**Допущения и предложения на листе**

Основа листа: размеры сняты со скана обмерного плана KV оформление (см): часть подписей не читается, помещения выровнены по читаемым размерам; контрольный обмер не выполнен (К-1); высота потолка 2650 мм принята по отметкам обмера (Н = 2,50…2,66 м, ригель 2,28 м) — уточнить при обмере (К-2); толщины стен 300 / 120 мм приняты, межквартирная стена и колонны — по скану, не замерены (К-1); разрешённая мощность 15 кВт принята по типовым ТУ; при объединении двух квартир — переоформление ТУ (К-4); подрайон климата не задан — принят не северный (жилые от 2,5 м) (К-8).

См. лист открытых вопросов (лист 6, записи К-1, К-2, К-4, К-8).

## Примечания

1. Развёртки — вид на стену изнутри помещения, по часовой стрелке; расположение — на схеме листа и на листе 79; размеры — в мм по чистовым поверхностям; отметки — в м от ±0,000; высоты Н — от чистого пола помещения до оси изделия, у декора — до центра.
2. Красная цепочка — привязки электроточек и выводов по осям от угла чистовых стен; высота Н — у знака, от чистого пола до оси; высоты мебели, проёмов и границ отделки — колонкой отметок слева. Стена с 5 и более точками или с мелкими звеньями привязок показана двумя видами: архитектурная развёртка (мебель, отделка, проёмы, высоты) и вид «Привязки» на отдельном листе — точки и выводы с марками, одна цепочка по осям и таблица привязок (каждая точка — строка).
3. У знака электроточки: марка (Р — розетка, S — выключатель, Св — светильник, ЭВ — вывод кабеля), ×N — число постов в рамке, гр. — группа щита, Н — высота оси от чистого пола, мм; группы по клавишам выключателя — на листе выключателей.
4. Схема мебели, приборов и декора не является технической документацией для производства мебели; габариты — по паспортам изделий (* — высота не задана в проекте, показана по типовому изделию).
5. Выводы ВК — коды и высоты по листу выводов сантехники; * — высота принята по типовой практике монтажа, окончательно — по паспорту прибора.
6. Двери скрытого монтажа — полотно в плоскости стены, отделка стены по полотну, плинтус прерывается у короба (узел — на листе узлов).

1000 мм · печать 1:1

| Изм. | Кол.уч | Лист | № док. | Подп. | Дата |
|---|---|---|---|---|---|
| Разраб. | | Кырлан А.С. | | | 04.11.26 |
| Пров. | | | | | |
| ГИП | | | | | |
| Н. контр. | | | | | |
| Утв. | | | | | |

**ГД-2026-009-АИ**

Квартира 103 м²

Общая площадь 100,72* м² · * размеры со скана, не замерены (реестр — л. 6, 7, К-1)

Дизайн-проект интерьера

| Стадия | Лист | Листов |
|---|---|---|
| РП | 98 | 120 |

**Развёртки стен. Постирочная (пом. 7)**

М 1:25

**Кырлан Александр Сергеевич**


выпуск 04.11.2026 № 35b47f1c2a · стр. 107 из 130

# Развёртки стен А, Б. Спальня 2 (пом. 8)

Спальня 2 (пом. 8) · вид изнутри помещения · размеры в мм, отметки в м


**ПРЕДВАРИТЕЛЬНО · не для производства работ · открыто пунктов: 8 (реестр — л. 6, 7)**

## Развёртка стены А

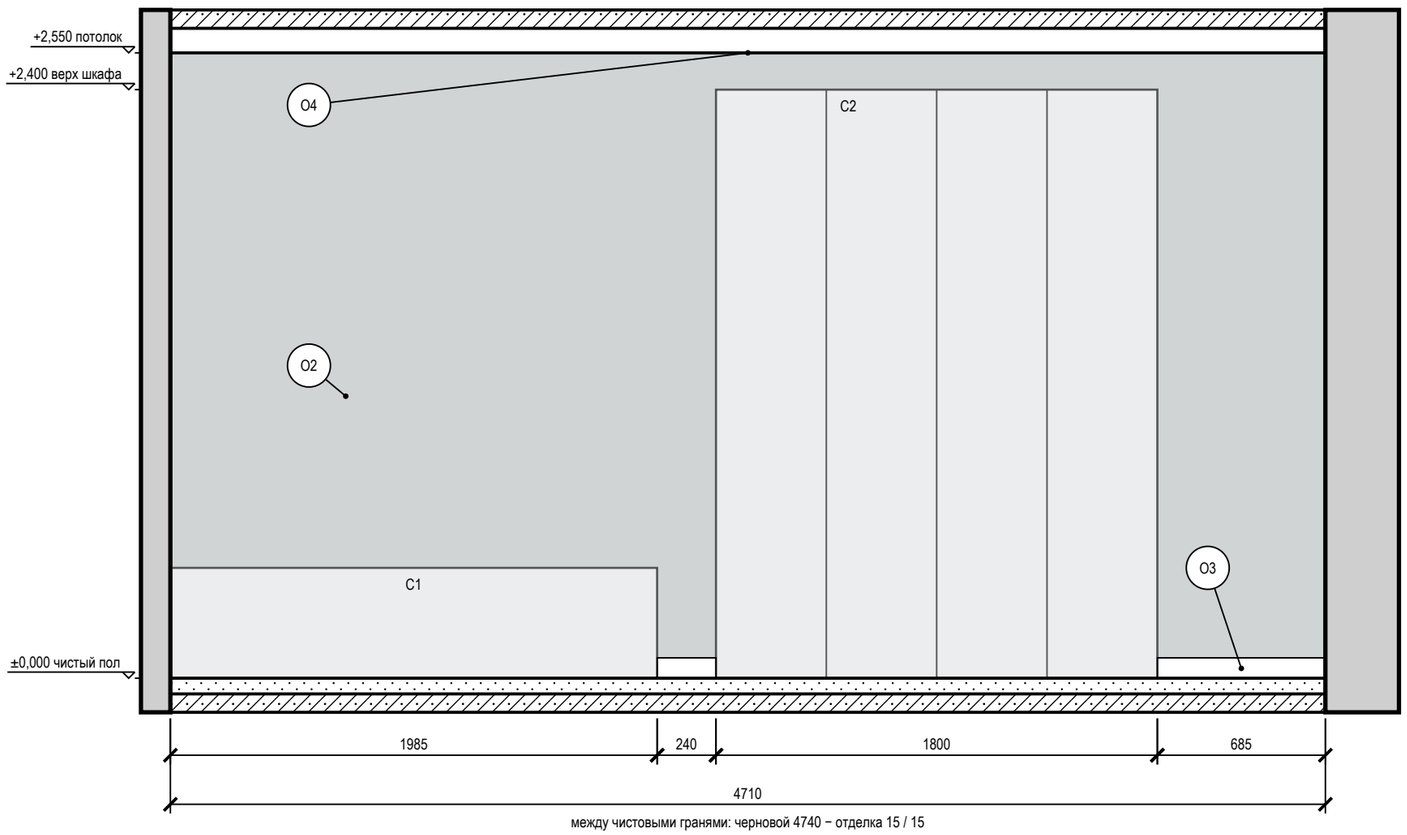



между чистовыми гранями: черновой 4740 − отделка 15 / 15

## Развёртка стены Б

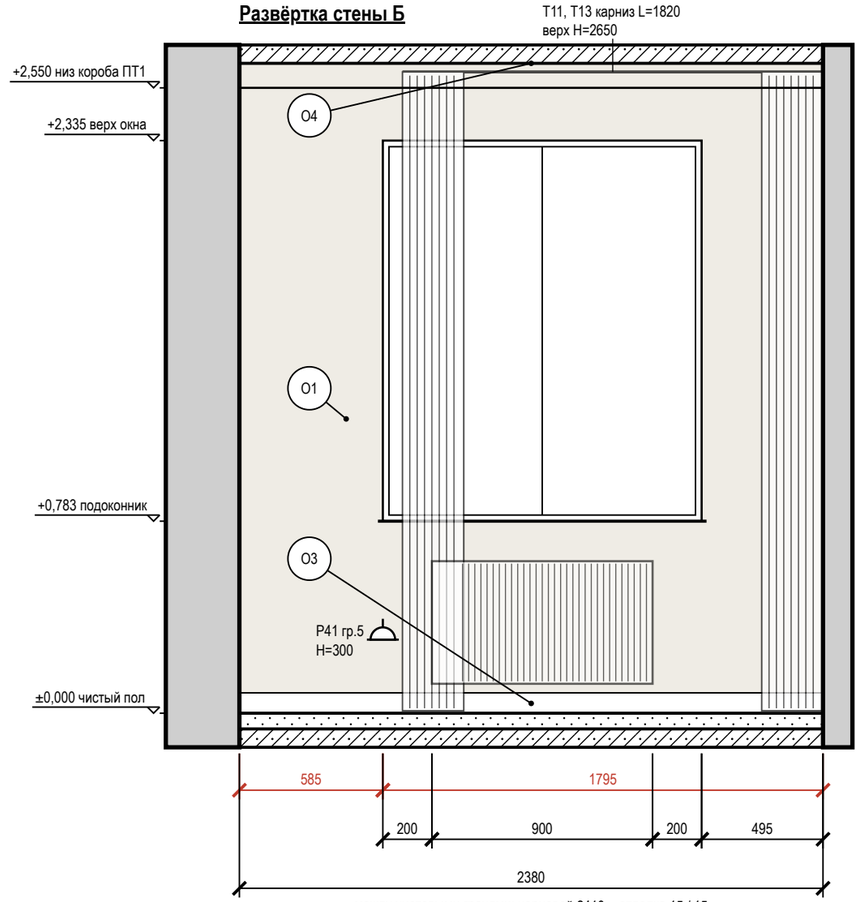


между чистовыми гранями: черновой 2410 − отделка 15 / 15

## Схема развёрток (М 1:100)

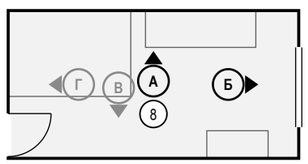


## Условные обозначения

- розетка с заземляющим контактом; у знака — марка, ×N постов в рамке, гр. — группа щита, Н — высота оси, мм
- привязки точек и выводов от угла и от пола, мм
- мебель и приборы — фасад по расстановке (условно)
- карниз (шина) и шторы в собранном виде: марка Т, длина L, верх Н
- окно: проём, рама, подоконник
- радиатор отопления; марка — по плану отопления
- стены и перекрытия в сечении
- окраска: тон — цвет по коду производителя (условно)
- О1 — марка отделки по реестру отделки альбома
- А — марка развёртки: буква стены, стрелка — взгляд

**Допущения и предложения на листе**

Основа листа: размеры сняты со скана обмерного плана KV оформление (см): часть подписей не читается, помещения выровнены по читаемым размерам; контрольный обмер не выполнен (К-1); высота потолка 2650 мм принята по отметкам обмера (Н = 2,50…2,66 м, ригель 2,28 м) — уточнить при обмере (К-2); толщины стен 300 / 120 мм приняты, межквартирная стена и колонны — по скану, не замерены (К-1); разрешённая мощность 15 кВт принята по типовым ТУ; при объединении двух квартир — переоформление ТУ (К-4); подрайон климата не задан — принят не северный (жилые от 2,5 м) (К-8).

См. лист открытых вопросов (лист 6, записи К-1, К-2, К-4, К-8).

## Примечания

1. Развёртки — вид на стену изнутри помещения, по часовой стрелке; расположение — на схеме листа и на листе 79; размеры — в мм по чистовым поверхностям; отметки — в м от ±0,000; высоты Н — от чистого пола помещения до оси изделия, у декора — до центра.
2. Красная цепочка — привязки электроточек и выводов по осям от угла чистовых стен; высота Н — у знака, от чистого пола до оси; высоты мебели, проёмов и границ отделки — колонкой отметок слева. Стена с 5 и более точками или с мелкими звеньями привязок показана двумя видами: архитектурная развёртка (мебель, отделка, проёмы, высоты) и вид «Привязки» на отдельном листе — точки и выводы с марками, одна цепочка по осям и таблица привязок (каждая точка — строка).
3. У знака электроточки: марка (Р — розетка, S — выключатель, Св — светильник, ЭВ — вывод кабеля), ×N — число постов в рамке, гр. — группа щита, Н — высота оси от чистого пола, мм; группы по клавишам выключателя — на листе выключателей.
4. Схема мебели, приборов и декора не является технической документацией для производства мебели; габариты — по паспортам изделий.
5. Карнизы (шины) — по ведомости текстиля декоратора: длина L и верх Н на развёртке — те же числа, что в ведомости; крепление — до окраски потолка.
6. Карниз Т11, Т13: по ведомости текстиля шина L=1820 мм, а от её начала до чистового угла стены — 1715 мм: шина не встаёт, длину согласовать с декоратором до заказа.
7. Линии узора (швы плитки, складки штор, рёбра радиаторов) прерываются у знаков и выносок — просвет между линиями не менее 0,7 мм.

1000 мм · печать 1:1

| Изм. | Кол.уч | Лист | № док. | Подп. | Дата |
|---|---|---|---|---|---|
| Разраб. | | Кырлан А.С. | | | 04.11.26 |
| Пров. | | | | | |
| ГИП | | | | | |
| Н. контр. | | | | | |
| Утв. | | | | | |

**ГД-2026-009-АИ**

Квартира 103 м²

Общая площадь 100,72* м² · * размеры со скана, не замерены (реестр — л. 6, 7, К-1)

Дизайн-проект интерьера

| Стадия | Лист | Листов |
|---|---|---|
| РП | 99 | 120 |

**Развёртки стен А, Б. Спальня 2 (пом. 8)**

М 1:25

**Кырлан Александр Сергеевич**


выпуск 04.11.2026 № 35b47f1c2a · стр. 108 из 130

# Развёртка стены В. Спальня 2 (пом. 8)

Спальня 2 (пом. 8) · вид изнутри помещения · размеры в мм, отметки в м


**ПРЕДВАРИТЕЛЬНО · не для производства работ · открыто пунктов: 8 (реестр — л. 6, 7)**

## Развёртка стены В

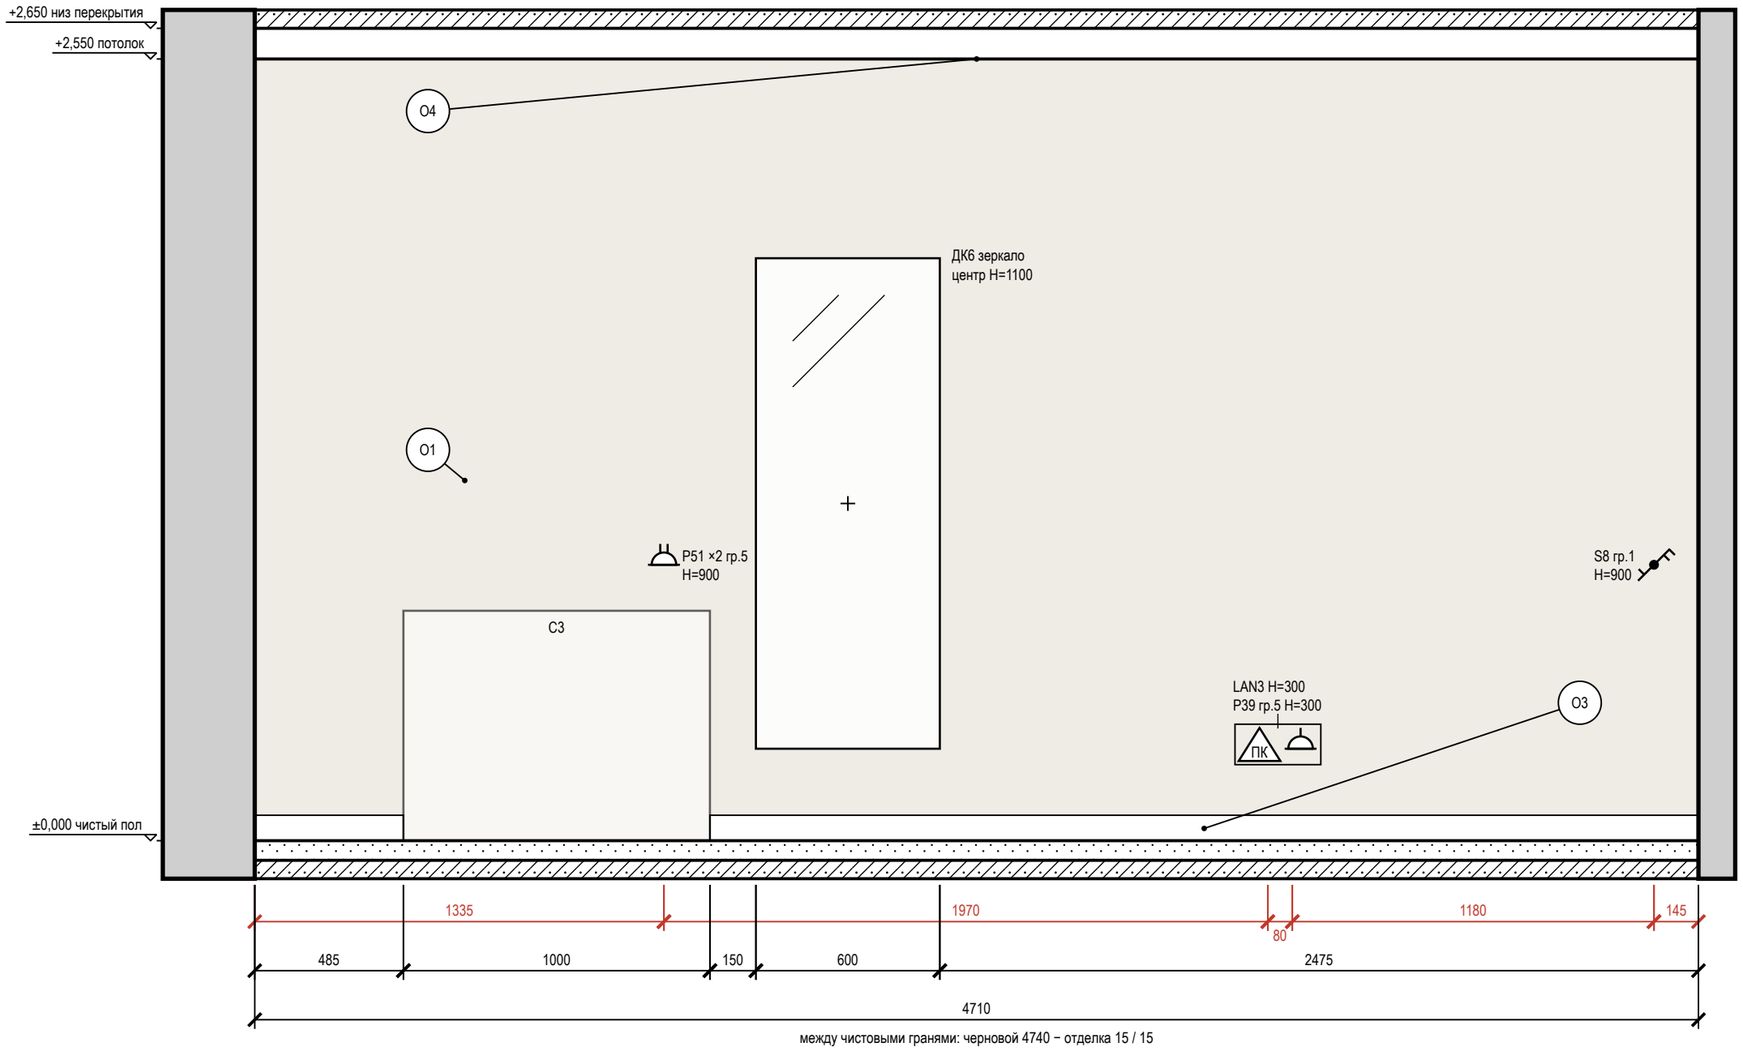


между чистовыми гранями: черновой 4740 − отделка 15 / 15

## Схема развёрток (М 1:100)

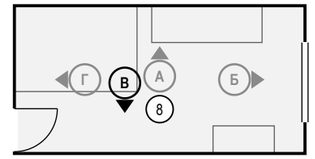


## Условные обозначения

- розетка с заземляющим контактом; у знака — марка, ×N постов в рамке, гр. — группа щита, Н — высота оси, мм
- выключатель одноклавишный
- выключатель двухклавишный (флажков — по числу клавиш)
- выключатель с проходной или перекрёстной клавишей (обратный флажок); тип клавиши — в подписи
- ПК — розетка компьютерная RJ45
- привязки точек и выводов от угла и от пола, мм
- мебель и приборы — фасад по расстановке (условно)
- зеркало: марка Д, крест — центр, Н — высота центра, мм
- стены и перекрытия в сечении
- окраска: тон — цвет по коду производителя (условно)
- О1 — марка отделки по реестру отделки альбома
- А — марка развёртки: буква стены, стрелка — взгляд

**Допущения и предложения на листе**

Основа листа: размеры сняты со скана обмерного плана KV оформление (см): часть подписей не читается, помещения выровнены по читаемым размерам; контрольный обмер не выполнен (К-1); высота потолка 2650 мм принята по отметкам обмера (Н = 2,50…2,66 м, ригель 2,28 м) — уточнить при обмере (К-2); толщины стен 300 / 120 мм приняты, межквартирная стена и колонны — по скану, не замерены (К-1); разрешённая мощность 15 кВт принята по типовым ТУ; при объединении двух квартир — переоформление ТУ (К-4); подрайон климата не задан — принят не северный (жилые от 2,5 м) (К-8).

См. лист открытых вопросов (лист 6, записи К-1, К-2, К-4, К-8).

## Примечания

1. Развёртки — вид на стену изнутри помещения, по часовой стрелке; расположение — на схеме листа и на листе 79; размеры — в мм по чистовым поверхностям; отметки — в м от ±0,000; высоты Н — от чистого пола помещения до оси изделия, у декора — до центра.
2. Красная цепочка — привязки электроточек и выводов по осям от угла чистовых стен; высота Н — у знака, от чистого пола до оси; высоты мебели, проёмов и границ отделки — колонкой отметок слева. Стена с 5 и более точками или с мелкими звеньями привязок показана двумя видами: архитектурная развёртка (мебель, отделка, проёмы, высоты) и вид «Привязки» на отдельном листе — точки и выводы с марками, одна цепочка по осям и таблица привязок (каждая точка — строка).
3. У знака электроточки: марка (Р — розетка, S — выключатель, Св — светильник, ЭВ — вывод кабеля), ×N — число постов в рамке, гр. — группа щита, Н — высота оси от чистого пола, мм; группы по клавишам выключателя — на листе выключателей.
4. Схема мебели, приборов и декора не является технической документацией для производства мебели; габариты — по паспортам изделий.
5. Картины и зеркала крепить к основанию по паспорту изделия (закладные и анкеры — в перечне скрытых работ); крест — ось центра предмета.

1000 мм · печать 1:1

| Изм. | Кол.уч | Лист | № док. | Подп. | Дата |
|---|---|---|---|---|---|
| Разраб. | | Кырлан А.С. | | | 04.11.26 |
| Пров. | | | | | |
| ГИП | | | | | |
| | | | | | |
| Н. контр. | | | | | |
| Утв. | | | | | |

**ГД-2026-009-АИ**

Квартира 103 м²

Общая площадь 100,72* м² · * размеры со скана, не замерены (реестр — л. 6, 7, К-1)

Дизайн-проект интерьера

| Стадия | Лист | Листов |
|---|---|---|
| РП | 100 | 120 |

**Развёртка стены В. Спальня 2 (пом. 8)**

М 1:20

**Кырлан Александр Сергеевич**


выпуск 04.11.2026 № 35b47f1c2a · стр. 109 из 130

# Развёртка стены Г. Спальня 2 (пом. 8)

Спальня 2 (пом. 8) · вид изнутри помещения · размеры в мм, отметки в м




## Развёртка стены Г

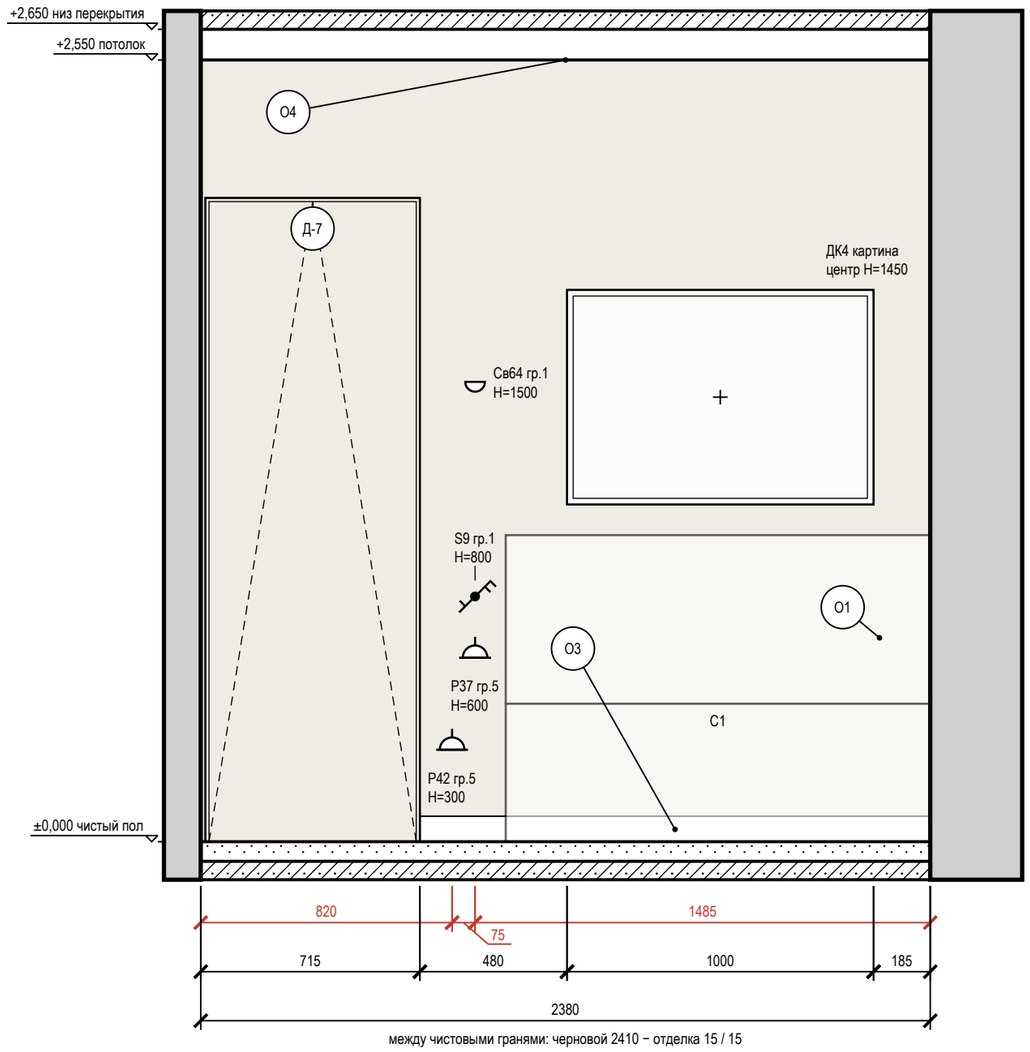


между чистовыми гранями: черновой 2410 − отделка 15 / 15

## Схема развёрток (М 1:100)

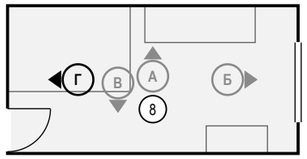


## Условные обозначения

- розетка с заземляющим контактом; у знака — марка, ×N постов в рамке, гр. — группа щита, Н — высота оси, мм
- выключатель одноклавишный
- выключатель двухклавишный (флажков — по числу клавиш)
- выключатель с проходной или перекрёстной клавишей (обратный флажок); тип клавиши — в подписи
- светильник настенный (бра), Н — высота оси
- привязки точек и выводов от угла и от пола, мм
- мебель и приборы — фасад по расстановке (условно)
- картина (декор): марка Д, крест — центр, Н — высота центра, мм
- дверь скрытого монтажа: полотно в плоскости стены (узел — на листе узлов)
- стены и перекрытия в сечении
- окраска: тон — цвет по коду производителя (условно)
- О1 — марка отделки по реестру отделки альбома
- А — марка развёртки: буква стены, стрелка — взгляд

## Ведомость отделки (на листе)

| Марка | Поверхность | Материал, изделие | Цвет, код | Кол. |
|---|---|---|---|---|
| О1 | стены | окраска, Farrow & Ball Modern Emulsion, матовая, подготовка Q3 | Farrow & Ball No. 291 «School House White тёплый меловой белый» | 4,6 м² |
| О3 | плинтус | плинтус МДФ, h 83 мм, Ultrawood Base 5340, ЛДФ под окраску, 83×15 мм, 2440 мм (арт. LDF-BASE-5340) | Farrow & Ball No. 291 «School House White тёплый меловой белый» | 1,7 м |
| О4 | потолок | окраска, Tikkurila Anti-Reflex 2, глубокоматовая, подготовка Q3 | NCS S 0502-Y «Белый с лёгкой желтизной» | 11,4 м² |

**Допущения и предложения на листе**

Основа листа: размеры сняты со скана обмерного плана KV оформление (см): часть подписей не читается, помещения выровнены по читаемым размерам; контрольный обмер не выполнен (К-1); высота потолка 2650 мм принята по отметкам обмера (Н = 2,50…2,66 м, ригель 2,28 м) — уточнить при обмере (К-2); толщины стен 300 / 120 мм приняты, межквартирная стена и колонны — по скану, не замерены (К-1); разрешённая мощность 15 кВт принята по типовым ТУ; при объединении двух квартир — переоформление ТУ (К-4); подрайон климата не задан — принят не северный (жилые от 2,5 м) (К-8).

См. лист открытых вопросов (лист 6, записи К-1, К-2, К-4, К-8).

## Примечания

1. Развёртки — вид на стену изнутри помещения, по часовой стрелке; расположение — на схеме листа и на листе 79; размеры — в мм по чистовым поверхностям; отметки — в м от ±0,000; высоты Н — от чистого пола помещения до оси изделия, у декора — до центра.
2. Красная цепочка — привязки электроточек и выводов по осям от угла чистовых стен; высота Н — у знака, от чистого пола до оси; высоты мебели, проёмов и границ отделки — колонкой отметок слева. Стена с 5 и более точками или с мелкими звеньями привязок показана двумя видами: архитектурная развёртка (мебель, отделка, проёмы, высоты) и вид «Привязки» на отдельном листе — точки и выводы с марками, одна цепочка по осям и таблица привязок (каждая точка — строка).
3. У знака электроточки: марка (Р — розетка, S — выключатель, Св — светильник, ЭВ — вывод кабеля), ×N — число постов в рамке, гр. — группа щита, Н — высота оси от чистого пола, мм; группы по клавишам выключателя — на листе выключателей.
4. Схема мебели, приборов и декора не является технической документацией для производства мебели; габариты — по паспортам изделий.
5. Картины и зеркала крепить к основанию по паспорту изделия (закладные и анкеры — в перечне скрытых работ); крест — ось центра предмета.
6. Двери скрытого монтажа — полотно в плоскости стены, отделка стены по полотну, плинтус прерывается у короба (узел — на листе узлов).

1000 мм · печать 1:1

| Изм. | Кол.уч | Лист | № док. | Подп. | Дата |
|---|---|---|---|---|---|
| Разраб. | | Кырлан А.С. | | | 04.11.26 |
| Пров. | | | | | |
| ГИП | | | | | |
| | | | | | |
| Н. контр. | | | | | |
| Утв. | | | | | |

**ГД-2026-009-АИ**

Квартира 103 м²

Общая площадь 100,72* м² · * размеры со скана, не замерены (реестр — л. 6, 7, К-1)

Дизайн-проект интерьера

| Стадия | Лист | Листов |
|---|---|---|
| РП | 101 | 120 |

**Развёртка стены Г. Спальня 2 (пом. 8)**

М 1:20

**Кырлан Александр Сергеевич**


выпуск 04.11.2026 № 35b47f1c2a · стр. 110 из 130

# Развёртка стены А. Коридор (пом. 9)

Коридор (пом. 9) · вид изнутри помещения · размеры в мм, отметки в м

**ПРЕДВАРИТЕЛЬНО · не для производства работ · открыто пунктов: 8 (реестр — л. 6, 7)**

**Развёртка стены А**

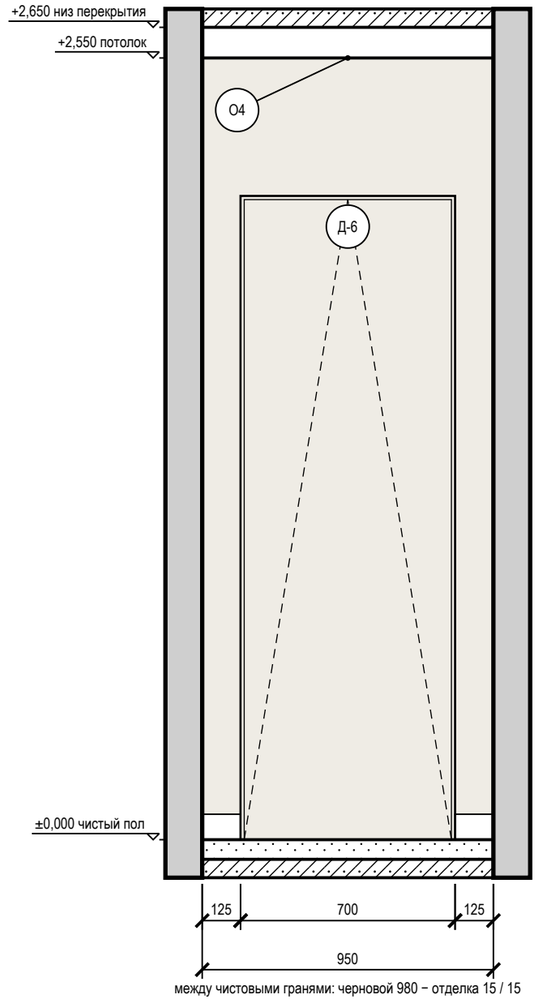


между чистовыми гранями: черновой 980 − отделка 15 / 15

## Схема развёрток (М 1:100)




## Условные обозначения

- мебель и приборы — фасад по расстановке (условно)
- дверь скрытого монтажа: полотно в плоскости стены (узел — на листе узлов)
- стены и перекрытия в сечении
- окраска: тон — цвет по коду производителя (условно)
- О1 — марка отделки по реестру отделки альбома
- А — марка развёртки: буква стены, стрелка — взгляд

## Ведомость отделки (на листе)

| Марка | Поверхность | Материал, изделие | Цвет, код | Кол. |
|---|---|---|---|---|
| О1 | стены | окраска, Farrow & Ball Modern Emulsion, матовая, подготовка Q3 | Farrow & Ball No. 291 «School House White — тёплый меловой белый» | 1 м² |
| О3 | плинтус | плинтус МДФ, h 83 мм, Ultrawood Base 5340, ЛДФ под окраску, 83×15 мм, 2440 мм (арт. LDF-BASE-5340) | Farrow & Ball No. 291 «School House White — тёплый меловой белый» | 0,3 м |
| О4 | потолок | окраска, Tikkurila Anti-Reflex 2, глубокоматовая, подготовка Q3 | NCS S 0502-Y «Белый с лёгкой желтизной» | 6 м² |

## Примечания

1. Развёртки — вид на стену изнутри помещения, по часовой стрелке; расположение — на схеме листа и на листе 79; размеры — в мм по чистовым поверхностям; отметки — в м от ±0,000; высоты Н — от чистого пола помещения до оси изделия, у декора — до центра.
2. Схема мебели, приборов и декора не является технической документацией для производства мебели; габариты — по паспортам изделий.
3. Двери скрытого монтажа — полотно в плоскости стены, отделка стены по полотну, плинтус прерывается у короба (узел — на листе узлов).

**Допущения и предложения на листе**

Основа листа: размеры сняты со скана обмерного плана KV оформление (см): часть подписей не читается, помещения выровнены по читаемым размерам; контрольный обмер не выполнен (К-1); высота потолка 2650 мм принята по отметкам обмера (Н = 2,50…2,66 м, ригель 2,28 м) — уточнить при обмере (К-2); толщины стен 300 / 120 мм приняты, межквартирная стена и колонны — по скану, не замерены (К-1); разрешённая мощность 15 кВт принята по типовым ТУ; при объединении двух квартир — переоформление ТУ (К-4); подрайон климата не задан — принят не северный (жилые от 2,5 м) (К-8).

См. лист открытых вопросов (лист 6, записи К-1, К-2, К-4, К-8).

1000 мм · печать 1:1

| Изм. | Кол.уч | Лист | № док. | Подп. | Дата |
|---|---|---|---|---|---|
| Разраб. | | Кырлан А.С. | | | 04.11.26 |
| Пров. | | | | | |
| ГИП | | | | | |
| | | | | | |
| Н. контр. | | | | | |
| Утв. | | | | | |

**ГД-2026-009-АИ**

Квартира 103 м²

Общая площадь 100,72* м² · * размеры со скана, не замерены (реестр — л. 6, 7, К-1)

Дизайн-проект интерьера

| Стадия | Лист | Листов |
|---|---|---|
| РП | 102 | 120 |

**Развёртка стены А. Коридор (пом. 9)**

М 1:20

**Кырлан Александр Сергеевич**


выпуск 04.11.2026 № 35b47f1c2a · стр. 111 из 130

# Развёртка стены Б. Коридор (пом. 9)

Коридор (пом. 9) · вид изнутри помещения · размеры в мм, отметки в м


ПРЕДВАРИТЕЛЬНО · не для производства работ · открыто пунктов: 8 (реестр — л. 6, 7)

## Развёртка стены Б

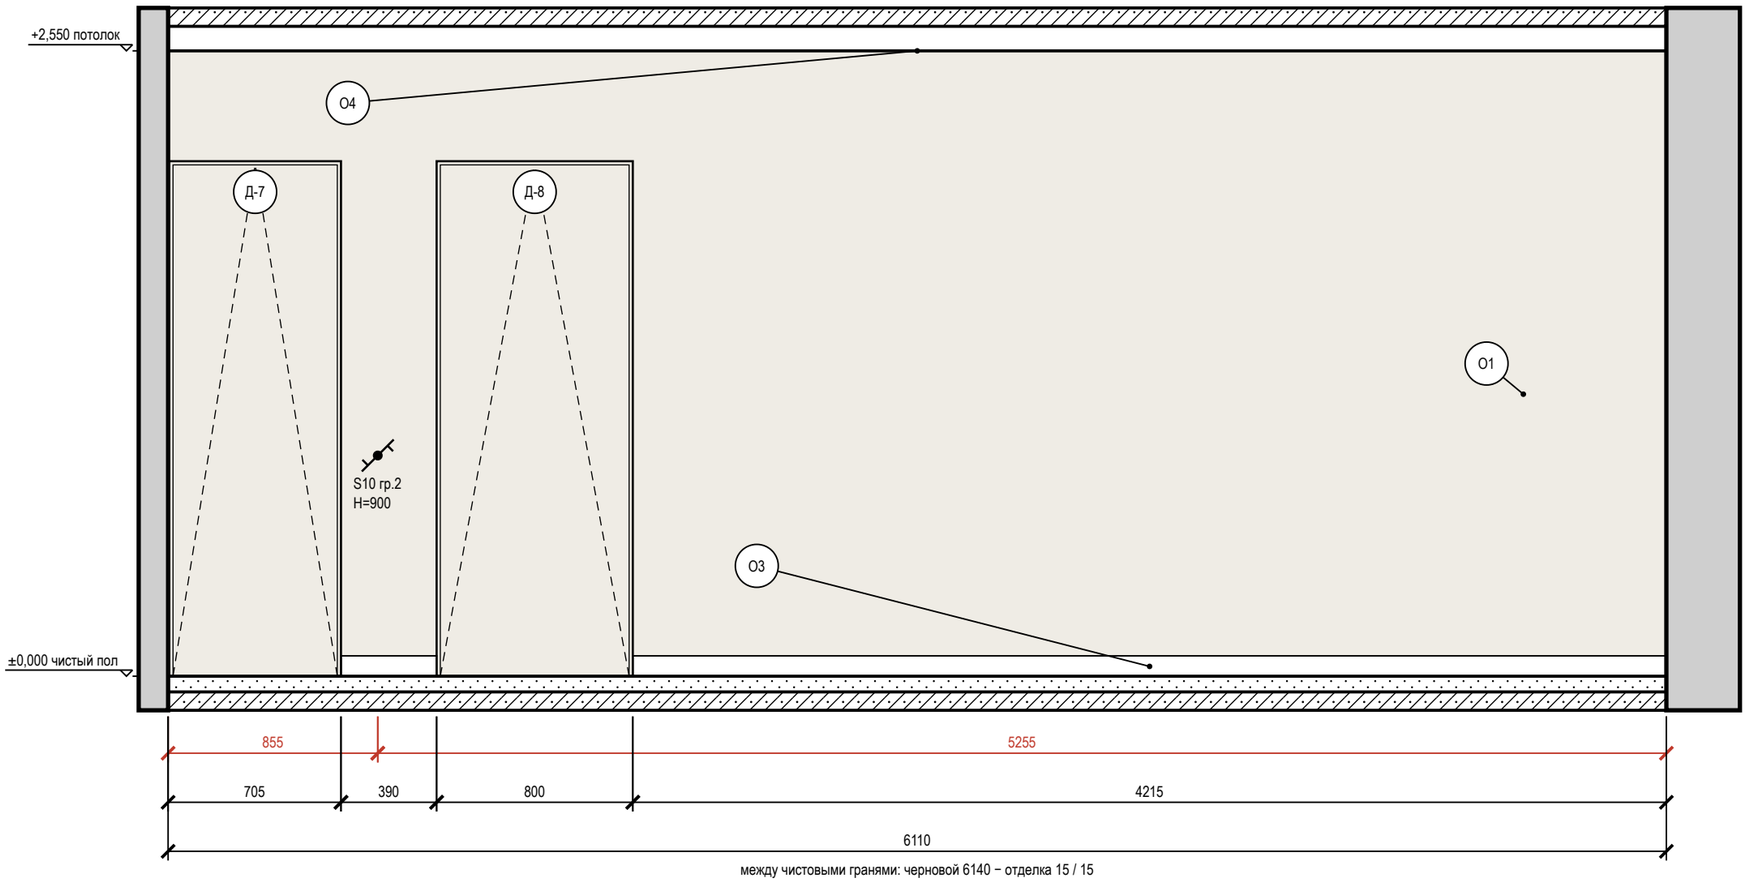


между чистовыми гранями: черновой 6140 − отделка 15 / 15

## Схема развёрток (М 1:100)

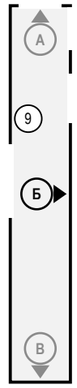


## Условные обозначения

- выключатель одноклавишный
- выключатель с проходной или перекрёстной клавишей (обратный флажок); тип клавиши — в подписи
- привязки точек и выводов от угла и от пола, мм
- мебель и приборы — фасад по расстановке (условно)
- дверь скрытого монтажа: полотно в плоскости стены (узел — на листе узлов)
- стены и перекрытия в сечении
- окраска: тон — цвет по коду производителя (условно)
- О1 — марка отделки по реестру отделки альбома
- А — марка развёртки: буква стены, стрелка — взгляд

## Ведомость отделки (на листе)

| Марка | Поверхность | Материал, изделие | Цвет, код | Кол. |
|---|---|---|---|---|
| О1 | стены | окраска, Farrow & Ball Modern Emulsion, матовая, подготовка Q3 | Farrow & Ball No. 291 «School House White тёплый меловой белый» | 12,4 м² |
| О3 | плинтус | плинтус МДФ, h 83 мм, Ultrawood Base 5340, ЛДФ под окраску, 83×15 мм, 2440 мм (арт. LDF-BASE-5340) | Farrow & Ball No. 291 «School House White тёплый меловой белый» | 4,6 м |
| О4 | потолок | окраска, Tikkurila Anti-Reflex 2, глубокоматовая, подготовка Q3 | NCS S 0502-Y «Белый с лёгкой желтизной» | 6 м² |

## Примечания

1. Развёртки — вид на стену изнутри помещения, по часовой стрелке; расположение — на схеме листа и на листе 79; размеры — в мм по чистовым поверхностям; отметки — в м от ±0,000; высоты Н — от чистого пола помещения до оси изделия, у декора — до центра.
2. Красная цепочка — привязки электроточек и выводов по осям от угла чистовых стен; высота Н — у знака, от чистого пола до оси; высоты мебели, проёмов и границ отделки — колонкой отметок слева. Стена с 5 и более точками или с мелкими звеньями привязок показана двумя видами: архитектурная развёртка (мебель, отделка, проёмы, высоты) и вид «Привязки» на отдельном листе — точки и выводы с марками, одна цепочка по осям и таблица привязок (каждая точка — строка).
3. У знака электроточки: марка (Р — розетка, S — выключатель, Св — светильник, ЭВ — вывод кабеля), ×N — число постов в рамке, гр. — группа щита, Н — высота оси от чистого пола, мм; группы по клавишам выключателя — на листе выключателей.
4. Схема мебели, приборов и декора не является технической документацией для производства мебели; габариты — по паспортам изделий.
5. Двери скрытого монтажа — полотно в плоскости стены, отделка стены по полотну, плинтус прерывается у короба (узел — на листе узлов).

1000 мм · печать 1:1

**Допущения и предложения на листе**

Основа листа: размеры сняты со скана обмерного плана KV оформление (см): часть подписей не читается, помещения выровнены по читаемым размерам; контрольный обмер не выполнен (К-1); высота потолка 2650 мм принята по отметкам обмера (Н = 2,50…2,66 м, ригель 2,28 м) — уточнить при обмере (К-2); толщины стен 300 / 120 мм приняты, межквартирная стена и колонны — по скану, не замерены (К-1); разрешённая мощность 15 кВт принята по типовым ТУ; при объединении двух квартир — переоформление ТУ (К-4); подрайон климата не задан — принят не северный (жилые от 2,5 м) (К-8).

См. лист открытых вопросов (лист 6, записи К-1, К-2, К-4, К-8).

| Изм. | Кол.уч | Лист | № док. | Подп. | Дата |
|---|---|---|---|---|---|
| Разраб. | | Кырлан А.С. | | | 04.11.26 |
| Пров. | | | | | |
| ГИП | | | | | |
| | | | | | |
| Н. контр. | | | | | |
| Утв. | | | | | |

**ГД-2026-009-АИ**

Квартира 103 м²

Общая площадь 100,72* м² · * размеры со скана, не замерены (реестр — л. 6, 7, К-1)

| Дизайн-проект интерьера | Стадия | Лист | Листов |
|---|---|---|---|
| | РП | 103 | 120 |

**Развёртка стены Б. Коридор (пом. 9)**

М 1:25

**Кырлан Александр Сергеевич**


выпуск 04.11.2026 № 35b47f1c2a · стр. 112 из 130

# Развёртка стены В. Коридор (пом. 9)

Коридор (пом. 9) · вид изнутри помещения · размеры в мм, отметки в м

**ПРЕДВАРИТЕЛЬНО · не для производства работ · открыто пунктов: 8 (реестр — л. 6, 7)**

## Развёртка стены В

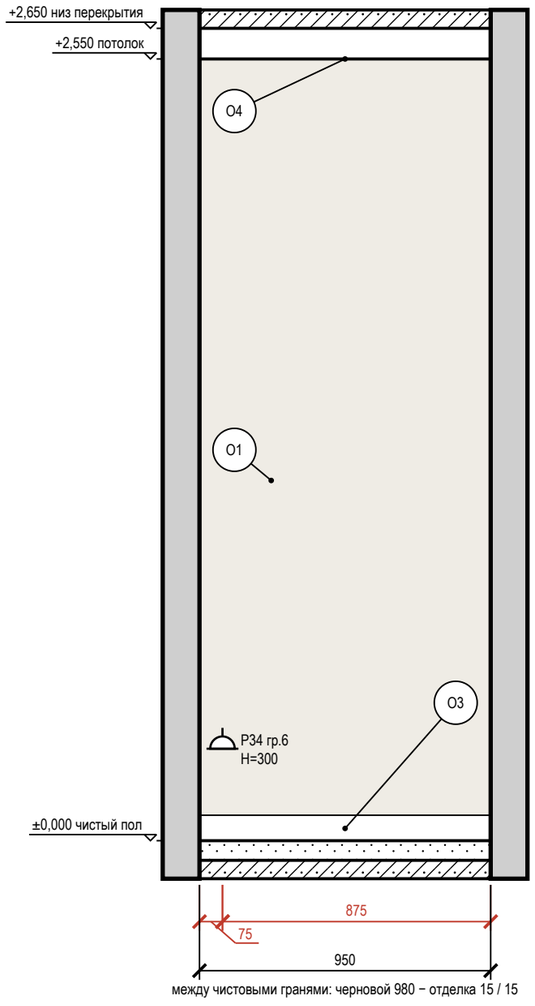


## Схема развёрток (М 1:100)




## Условные обозначения

- розетка с заземляющим контактом; у знака — марка, ×N постов в рамке, гр. — группа щита, Н — высота оси, мм
- привязки точек и выводов от угла и от пола, мм
- мебель и приборы — фасад по расстановке (условно)
- стены и перекрытия в сечении
- окраска: тон — цвет по коду производителя (условно)
- О1 — марка отделки по реестру отделки альбома
- А — марка развёртки: буква стены, стрелка — взгляд

## Ведомость отделки (на листе)

| Марка | Поверхность | Материал, изделие | Цвет, код | Кол. |
|---|---|---|---|---|
| О1 | стены | окраска, Farrow & Ball Modern Emulsion, матовая, подготовка Q3 | Farrow & Ball No. 291 «School House White тёплый меловой белый» | 2,4 м² |
| О3 | плинтус | плинтус МДФ, h 83 мм, Ultrawood Base 5340, ЛДФ под окраску, 83×15 мм, 2440 мм (арт. LDF-BASE-5340) | Farrow & Ball No. 291 «School House White тёплый меловой белый» | 0,9 м |
| О4 | потолок | окраска, Tikkurila Anti-Reflex 2, глубокоматовая, подготовка Q3 | NCS S 0502-Y «Белый с лёгкой желтизной» | 6 м² |

**Допущения и предложения на листе**

Основа листа: размеры сняты со скана обмерного плана KV оформление (см): часть подписей не читается, помещения выровнены по читаемым размерам; контрольный обмер не выполнен (К-1); высота потолка 2650 мм принята по отметкам обмера (Н = 2,50…2,66 м, ригель 2,28 м) — уточнить при обмере (К-2); толщины стен 300 / 120 мм приняты, межквартирная стена и колонны — по скану, не замерены (К-1); разрешённая мощность 15 кВт принята по типовым ТУ; при объединении двух квартир — переоформление ТУ (К-4); подрайон климата не задан — принят не северный (жилые от 2,5 м) (К-8).

См. лист открытых вопросов (лист 6, записи К-1, К-2, К-4, К-8).

## Примечания

1. Развёртки — вид на стену изнутри помещения, по часовой стрелке; расположение — на схеме листа и на листе 79; размеры — в мм по чистовым поверхностям; отметки — в м от ±0,000; высоты Н — от чистого пола помещения до оси изделия, у декора — до центра.
2. Красная цепочка — привязки электроточек и выводов по осям от угла чистовых стен; высота Н — у знака, от чистого пола до оси; высоты мебели, проёмов и границ отделки — колонкой отметок слева. Стена с 5 и более точками или с мелкими звеньями привязок показана двумя видами: архитектурная развёртка (мебель, отделка, проёмы, высоты) и вид «Привязки» на отдельном листе — точки и выводы с марками, одна цепочка по осям и таблица привязок (каждая точка — строка).
3. У знака электроточки: марка (Р — розетка, S — выключатель, Св — светильник, ЭВ — вывод кабеля), ×N — число постов в рамке, гр. — группа щита, Н — высота оси от чистого пола, мм; группы по клавишам выключателя — на листе выключателей.
4. Схема мебели, приборов и декора не является технической документацией для производства мебели; габариты — по паспортам изделий.

1000 мм · печать 1:1

| Изм. | Кол.уч | Лист | № док. | Подп. | Дата |
|---|---|---|---|---|---|
| Разраб. | | Кырлан А.С. | | | 04.11.26 |
| Пров. | | | | | |
| ГИП | | | | | |
| | | | | | |
| Н. контр. | | | | | |
| Утв. | | | | | |

**ГД-2026-009-АИ**

Квартира 103 м²

Общая площадь 100,72* м² · * размеры со скана, не замерены (реестр — л. 6, 7, К-1)

Дизайн-проект интерьера

| Стадия | Лист | Листов |
|---|---|---|
| РП | 104 | 120 |

**Развёртка стены В. Коридор (пом. 9)**

М 1:20

**Кырлан Александр Сергеевич**


выпуск 04.11.2026 № 35b47f1c2a · стр. 113 из 130

# Развёртка стены А. Спальня мастер (пом. 10)

Спальня мастер (пом. 10) · вид изнутри помещения · размеры в мм, отметки в м


**ПРЕДВАРИТЕЛЬНО · не для производства работ · открыто пунктов: 8 (реестр — л. 6, 7)**

## Развёртка стены А

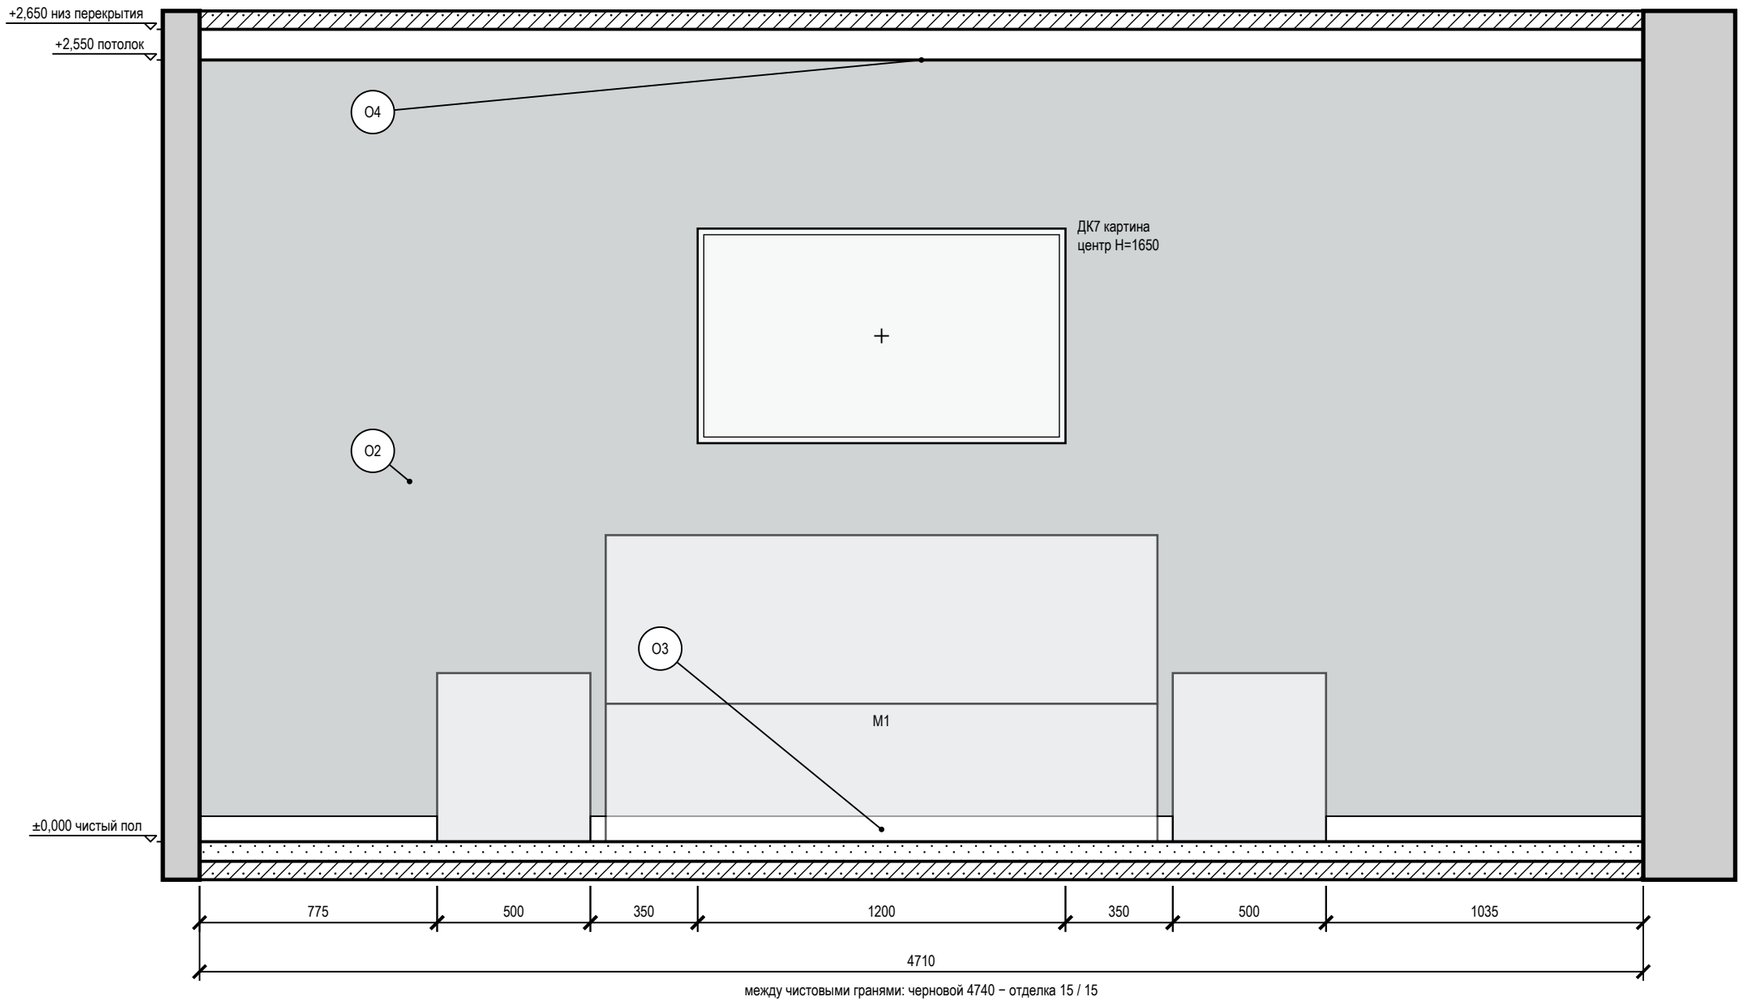


между чистовыми гранями: черновой 4740 − отделка 15 / 15

## Схема развёрток (М 1:100)

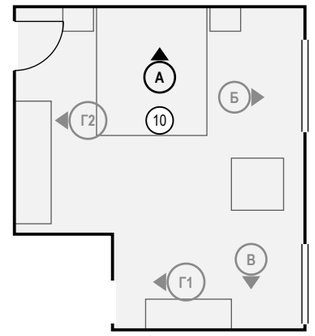


## Условные обозначения

- мебель и приборы — фасад по расстановке (условно)
- картина (декор): марка Д, крест — центр, Н — высота центра, мм
- стены и перекрытия в сечении
- окраска: тон — цвет по коду производителя (условно)
- О1 — марка отделки по реестру отделки альбома
- А — марка развёртки: буква стены, стрелка — взгляд

**Допущения и предложения на листе**

Основа листа: размеры сняты со скана обмерного плана KV оформление (см): часть подписей не читается, помещения выровнены по читаемым размерам; контрольный обмер не выполнен (К-1); высота потолка 2650 мм принята по отметкам обмера (Н = 2,50…2,66 м, ригель 2,28 м) — уточнить при обмере (К-2); толщины стен 300 / 120 мм приняты, межквартирная стена и колонны — по скану, не замерены (К-1); разрешённая мощность 15 кВт принята по типовым ТУ; при объединении двух квартир — переоформление ТУ (К-4); подрайон климата не задан — принят не северный (жилые от 2,5 м) (К-8).

Знак «*» — принято, не замерено и не подтверждено (замерить на объекте): К-1: окно пом. 10 (стена Б) — Окно 1300 при смещение 3500 на стене Б основной части (длина 3830) выходило за стену на 970 мм.

См. лист открытых вопросов (лист 6, записи К-1, К-2, К-4, К-8).

## Примечания

1. Развёртки — вид на стену изнутри помещения, по часовой стрелке; расположение — на схеме листа и на листе 79; размеры — в мм по чистовым поверхностям; отметки — в м от ±0,000; высоты Н — от чистого пола помещения до оси изделия, у декора — до центра.
2. Стена А показана двумя видами: здесь — архитектурная развёртка (мебель, отделка, проёмы, высоты), электроточки и выводы ВК с привязками и таблицей — на листе 106 («Привязки»).
3. Схема мебели, приборов и декора не является технической документацией для производства мебели; габариты — по паспортам изделий.
4. Картины и зеркала крепить к основанию по паспорту изделия (закладные и анкеры — в перечне скрытых работ); крест — ось центра предмета.

1000 мм · печать 1:1

| Изм. | Кол.уч | Лист | № док. | Подп. | Дата |
|---|---|---|---|---|---|
| Разраб. | | Кырлан А.С. | | | 04.11.26 |
| Пров. | | | | | |
| ГИП | | | | | |
| Н. контр. | | | | | |
| Утв. | | | | | |

**ГД-2026-009-АИ**

Квартира 103 м²

Общая площадь 100,72* м² · * размеры со скана, не замерены (реестр — л. 6, 7, К-1)

Дизайн-проект интерьера

| Стадия | Лист | Листов |
|---|---|---|
| РП | 105 | 120 |

**Развёртка стены А. Спальня мастер (пом. 10)**

М 1:20

**Кырлан Александр Сергеевич**


выпуск 04.11.2026 № 35b47f1c2a · стр. 114 из 130

# Привязки электроточек, стена А. Спальня мастер (пом. 10)

Спальня мастер (пом. 10) · вид изнутри помещения · привязки в мм, отметки в м · к развёртке на листе 105

ПРЕДВАРИТЕЛЬНО · не для производства работ · открыто пунктов: 8 (реестр — л. 6, 7)

## Развёртка стены А: электроточки и выводы

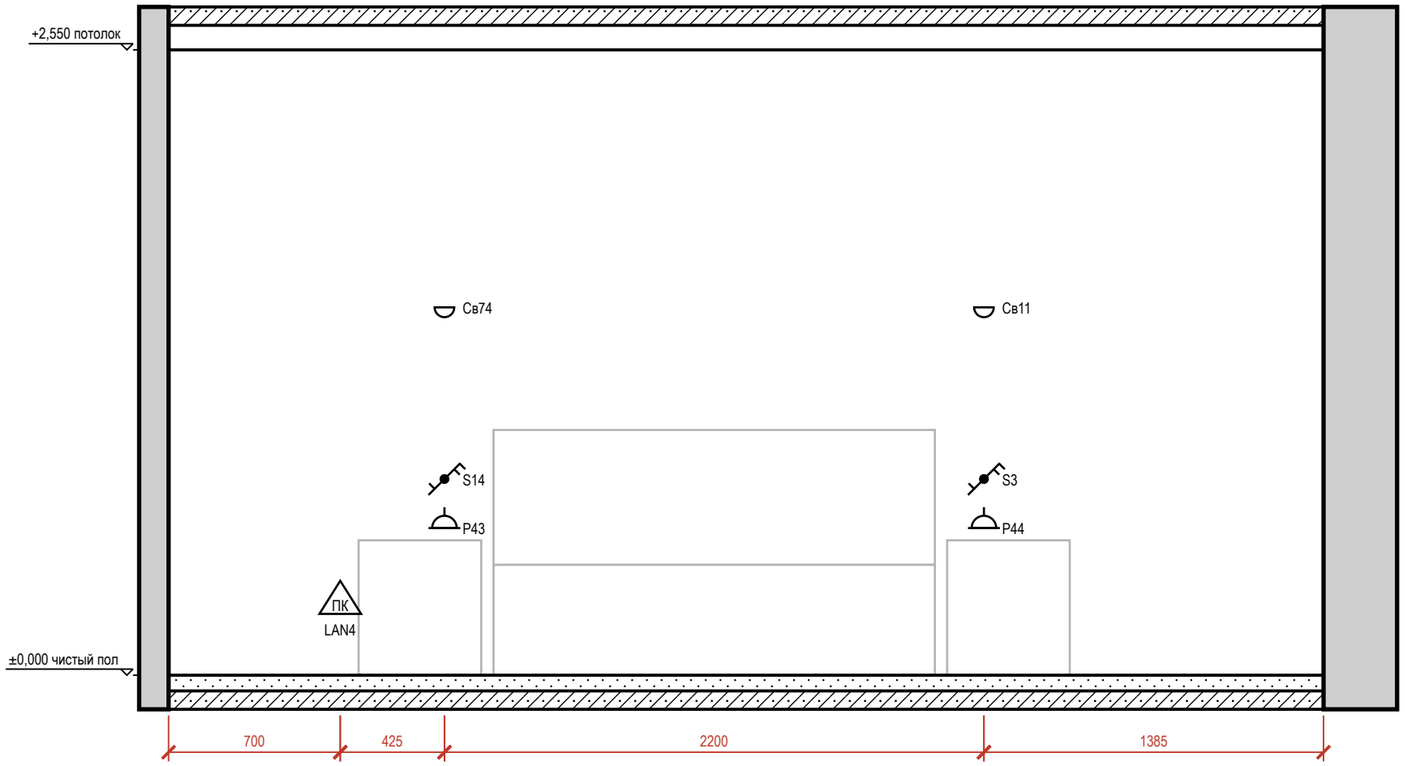



## Таблица привязок электроточек и выводов

| Марка | Назначение | От угла, мм | Н от пола, мм | Примечание |
|---|---|---|---|---|
| LAN4 | розетка RJ45: передача данных | 700 | 300 | |
| P43 | розетка: у кровати | 1125 | 600 | гр. 4 |
| S14 | выключатель | 1125 | 800 | гр. 1 |
| Св74 | светильник настенный | 1125 | 1500 | гр. 1 |
| P44 | розетка: у кровати | 3325 | 600 | гр. 4 |
| S3 | выключатель | 3325 | 800 | гр. 1 |
| Св11 | светильник настенный | 3325 | 1500 | гр. 1 |

## Условные обозначения

- розетка с заземляющим контактом; у знака — марка, ×N постов в рамке, гр. — группа щита, Н — высота оси, мм
- выключатель одноклавишный
- выключатель двухклавишный (флажков — по числу клавиш)
- выключатель с проходной или перекрёстной клавишей (обратный флажок); тип клавиши — в подписи
- светильник настенный (бра), Н — высота оси
- ПК — розетка компьютерная RJ45
- привязки точек и выводов от угла и от пола, мм
- А — марка развёртки: буква стены, стрелка — взгляд

## Схема развёрток (М 1:200)

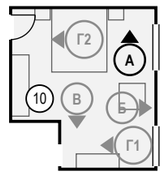


## Примечания

1. Вид «Привязки» стены А — электроточки и выводы ВК; архитектурная развёртка (мебель, отделка, проёмы, высоты) — на листе 105, расположение — на листе 79. Мебель и приборы — подложкой для ориентира; их марки и обозначения мебели, проёмов и стен — там же.
2. Привязки — в мм: по горизонтали от левого чистового угла стены до оси изделия, Н — от чистого пола до оси; все точки — в таблице привязок. Красная цепочка — привязки по осям; точки ближе 150 мм одна к другой в цепочку не дробятся — их привязки только в таблице.
3. У знака — марка электроточки (Р — розетка, S — выключатель, Св — светильник, ЭВ — вывод кабеля); посты в рамке и группа щита — в графе «Примечание»; группы по клавишам выключателя — на листе выключателей.

**Допущения и предложения на листе**

Основа листа: размеры сняты со скана обмерного плана KV оформление (см): часть подписей не читается, помещения выровнены по читаемым размерам; контрольный обмер не выполнен (К-1); высота потолка 2650 мм принята по отметкам обмера (Н = 2,50…2,66 м, ригель 2,28 м) — уточнить при обмере (К-2); толщины стен 300 / 120 мм приняты, межквартирная стена и колонны — по скану, не замерены (К-1); разрешённая мощность 15 кВт принята по типовым ТУ; при объединении двух квартир — переоформление ТУ (К-4); подрайон климата не задан — принят не северный (жилые от 2,5 м) (К-8).

Знак «*» — принято, не замерено и не подтверждено (замерить на объекте): К-1: окно пом. 10 (стена Б) — Окно 1300 при смещение 3500 на стене Б основной части (длина 3830) выходило за стену на 970 мм.

См. лист открытых вопросов (лист 6, записи К-1, К-2, К-4, К-8).

1000 мм · печать 1:1

| Изм. | Кол.уч | Лист | № док. | Подп. | Дата |
|---|---|---|---|---|---|
| Разраб. | | Кырлан А.С. | | | 04.11.26 |
| Пров. | | | | | |
| ГИП | | | | | |
| | | | | | |
| Н. контр. | | | | | |
| Утв. | | | | | |

**ГД-2026-009-АИ**

Квартира 103 м²

Общая площадь 100,72* м² · * размеры со скана, не замерены (реестр — л. 6, 7, К-1)

| Дизайн-проект интерьера | Стадия | Лист | Листов |
|---|---|---|---|
| | РП | 106 | 120 |

**Привязки электроточек, стена А. Спальня мастер (пом. 10)**

М 1:25

**Кырлан Александр Сергеевич**


выпуск 04.11.2026 № 35b47f1c2a · стр. 115 из 130

# Развёртка стены Б. Спальня мастер (пом. 10)

Спальня мастер (пом. 10) · вид изнутри помещения · размеры в мм, отметки в м


ПРЕДВАРИТЕЛЬНО · не для производства работ · открыто пунктов: 8 (реестр — л. 6, 7)

## Развёртка стены Б

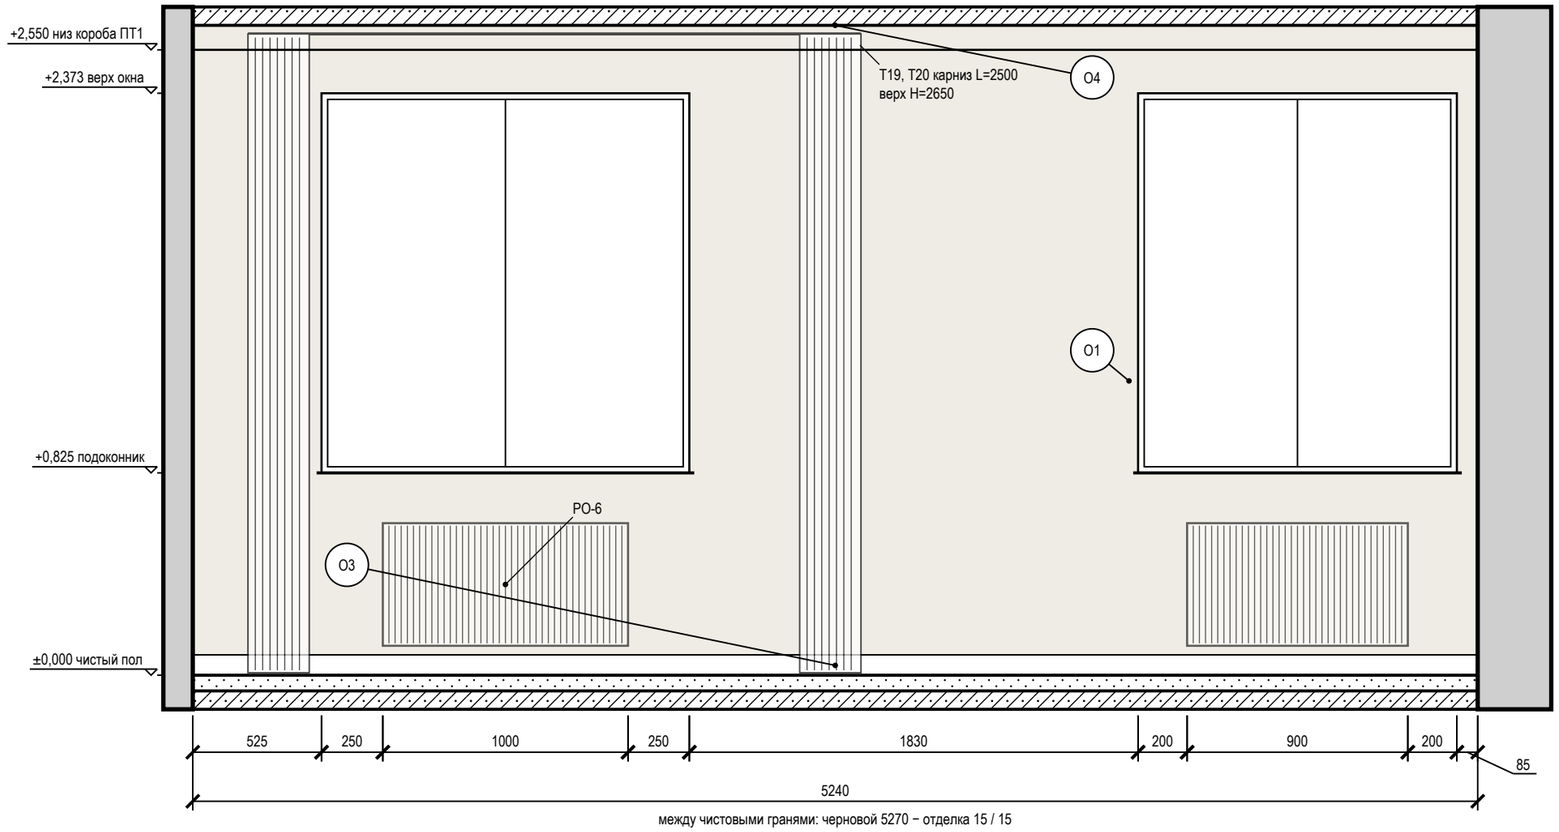


между чистовыми гранями: черновой 5270 − отделка 15 / 15

## Схема развёрток (М 1:100)

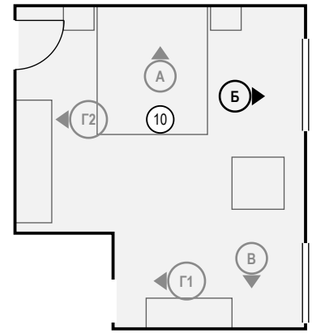


## Условные обозначения

- мебель и приборы — фасад по расстановке (условно)
- карниз (шина) и шторы в собранном виде: марка Т, длина L, верх H
- окно: проём, рама, подоконник
- радиатор отопления; марка — по плану отопления
- стены и перекрытия в сечении
- окраска: тон — цвет по коду производителя (условно)
- О1 — марка отделки по реестру отделки альбома
- А — марка развёртки: буква стены, стрелка — взгляд

## Ведомость отделки (на листе)

| Марка | Поверхность | Материал, изделие | Цвет, код | Кол. |
|---|---|---|---|---|
| О1 | стены | окраска, Farrow & Ball Modern Emulsion, матовая, подготовка Q3 | Farrow & Ball No. 291 «School House White — тёплый меловой белый» | 9,6 м² |
| О3 | плинтус | плинтус МДФ, h 83 мм, Ultrawood Base 5340, ЛДФ под окраску, 83×15 мм, 2440 мм (арт. LDF-BASE-5340) | Farrow & Ball No. 291 «School House White — тёплый меловой белый» | 5,2 м |
| О4 | потолок | окраска, Tikkurila Anti-Reflex 2, глубокоматовая, подготовка Q3 | NCS S 0502-Y «Белый с лёгкой желтизной» | 22,5 м² |

**Допущения и предложения на листе**

Основа листа: размеры сняты со скана обмерного плана KV оформление (см): часть подписей не читается, помещения выровнены по читаемым размерам; контрольный обмер не выполнен (К-1); высота потолка 2650 мм принята по отметкам обмера (Н = 2,50…2,66 м, ригель 2,28 м) — уточнить при обмере (К-2); толщины стен 300 / 120 мм приняты, межквартирная стена и колонны — по скану, не замерены (К-1); разрешённая мощность 15 кВт принята по типовым ТУ; при объединении двух квартир — переоформление ТУ (К-4); подрайон климата не задан — принят не северный (жилые от 2,5 м) (К-8).

Знак «*» — принято, не замерено и не подтверждено (замерить на объекте): К-1: окно пом. 10 (стена Б) — Окно 1300 при смещение 3500 на стене Б основной части (длина 3830) выходило за стену на 970 мм.

См. лист открытых вопросов (лист 6, записи К-1, К-2, К-4, К-8).

## Примечания

1. Развёртки — вид на стену изнутри помещения, по часовой стрелке; расположение — на схеме листа и на листе 79; размеры — в мм по чистовым поверхностям; отметки — в м от ±0,000; высоты Н — от чистого пола помещения до оси изделия, у декора — до центра.
2. Схема мебели, приборов и декора не является технической документацией для производства мебели; габариты — по паспортам изделий.
3. Карнизы (шины) — по ведомости текстиля декоратора: длина L и верх Н на развёртке — те же числа, что в ведомости; крепление — до окраски потолка.

1000 мм · печать 1:1

| Изм. | Кол.уч | Лист | № док. | Подп. | Дата |
|---|---|---|---|---|---|
| Разраб. | | Кырлан А.С. | | | 04.11.26 |
| Пров. | | | | | |
| ГИП | | | | | |
| Н. контр. | | | | | |
| Утв. | | | | | |

**ГД-2026-009-АИ**

Квартира 103 м²

Общая площадь 100,72* м² · * размеры со скана, не замерены (реестр — л. 6, 7, К-1)

Дизайн-проект интерьера

| Стадия | Лист | Листов |
|---|---|---|
| РП | 107 | 120 |

**Развёртка стены Б. Спальня мастер (пом. 10)**

М 1:25

**Кырлан Александр Сергеевич**


выпуск 04.11.2026 № 35b47f1c2a · стр. 116 из 130

# Развёртки стен В, Г1. Спальня мастер (пом. 10)

Спальня мастер (пом. 10) · вид изнутри помещения · размеры в мм, отметки в м


ПРЕДВАРИТЕЛЬНО · не для производства работ · открыто пунктов: 8 (реестр — л. 6, 7)

## Развёртка стены В

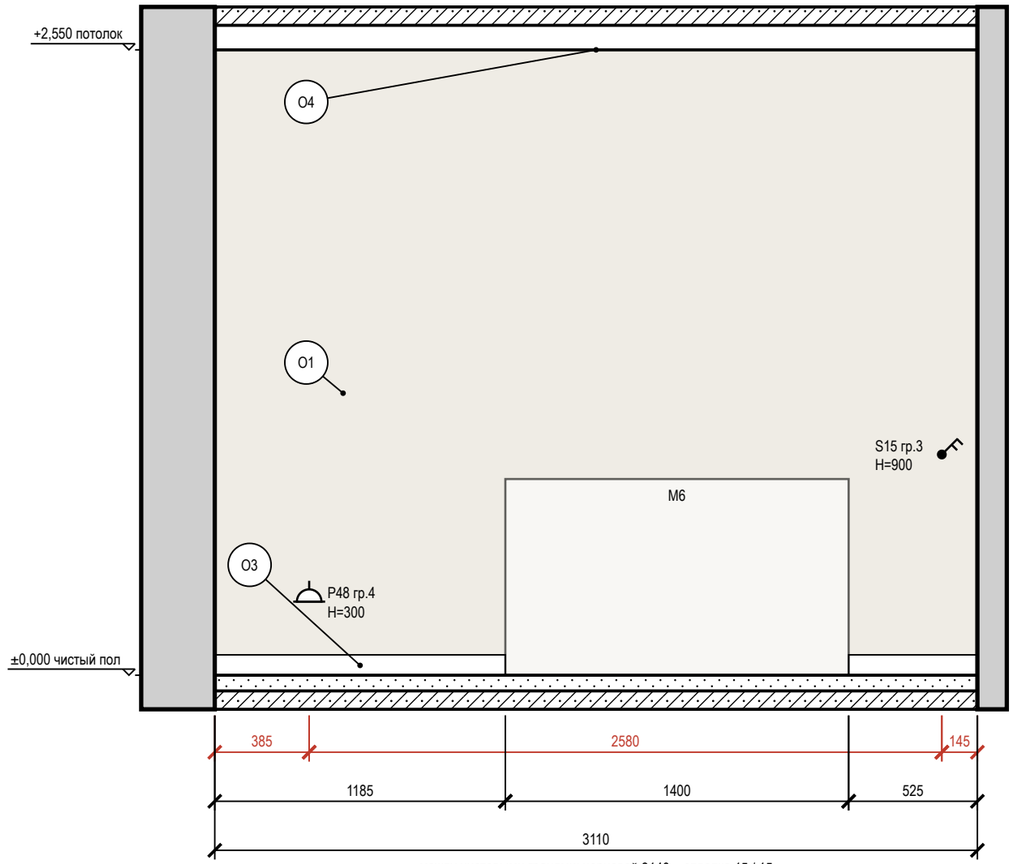



между чистовыми гранями: черновой 3140 − отделка 15 / 15

## Развёртка стены Г1

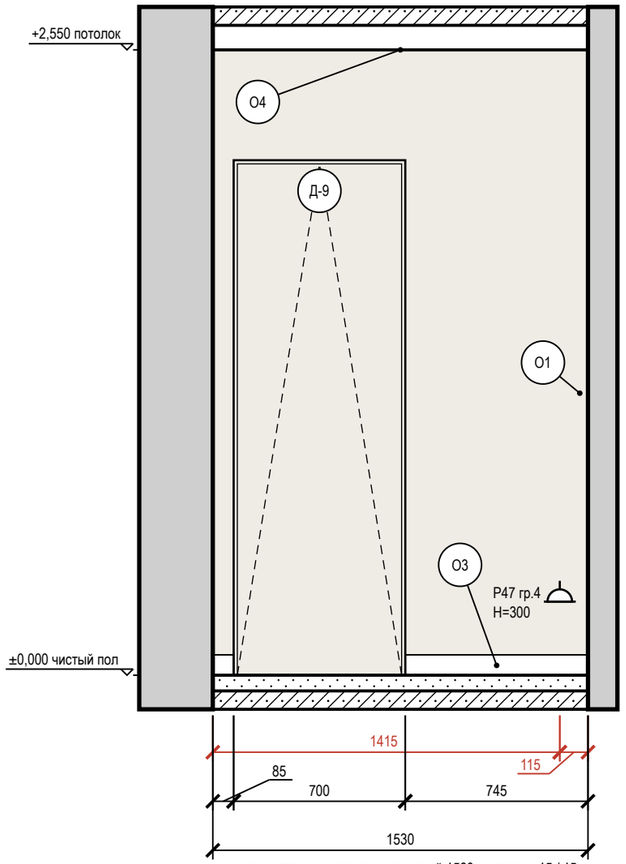


между чистовыми гранями: черновой 1560 − отделка 15 / 15

## Схема развёрток (М 1:100)

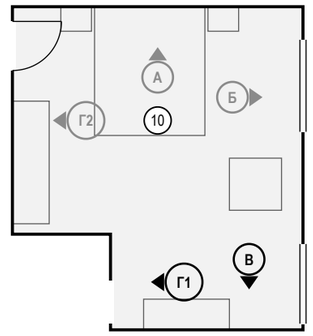


## Условные обозначения

- розетка с заземляющим контактом; у знака — марка, ×N постов в рамке, гр. — группа щита, Н — высота оси, мм
- выключатель одноклавишный
- выключатель двухклавишный (флажков — по числу клавиш)
- привязки точек и выводов от угла и от пола, мм
- мебель и приборы — фасад по расстановке (условно)
- дверь скрытого монтажа: полотно в плоскости стены (узел — на листе узлов)
- стены и перекрытия в сечении
- окраска: тон — цвет по коду производителя (условно)
- О1 — марка отделки по реестру отделки альбома
- А — марка развёртки: буква стены, стрелка — взгляд

## Ведомость отделки (на листе)

| Марка | Поверхность | Материал, изделие | Цвет, код | Кол. |
|---|---|---|---|---|
| О1 | стены | окраска, Farrow & Ball Modern Emulsion, матовая, подготовка Q3 | Farrow & Ball No. 291 «School House White тёплый меловой белый» | 10,4 м² |
| О3 | плинтус | плинтус МДФ, h 83 мм, Ultrawood Base 5340, ЛДФ под окраску, 83×15 мм, 2440 мм (арт. LDF-BASE-5340) | Farrow & Ball No. 291 «School House White тёплый меловой белый» | 2,5 м |
| О4 | потолок | окраска, Tikkurila Anti-Reflex 2, глубокоматовая, подготовка Q3 | NCS S 0502-Y «Белый с лёгкой желтизной» | 22,5 м² |

## Примечания

1. Развёртки — вид на стену изнутри помещения, по часовой стрелке; расположение — на схеме листа и на листе 79; размеры — в мм по чистовым поверхностям; отметки — в м от ±0,000; высоты Н — от чистого пола помещения до оси изделия, у декора — до центра.
2. Красная цепочка — привязки электроточек и выводов по осям от угла чистовых стен; высота Н — у знака, от чистого пола до оси; высоты мебели, проёмов и границ отделки — колонкой отметок слева. Стена с 5 и более точками или с мелкими звеньями привязок показана двумя видами: архитектурная развёртка (мебель, отделка, проёмы, высоты) и вид «Привязки» на отдельном листе — точки и выводы с марками, одна цепочка по осям и таблица привязок (каждая точка — строка).
3. У знака электроточки: марка (Р — розетка, S — выключатель, Св — светильник, ЭВ — вывод кабеля), ×N — число постов в рамке, гр. — группа щита, Н — высота оси от чистого пола, мм; группы по клавишам выключателя — на листе выключателей.
4. Схема мебели, приборов и декора не является технической документацией для производства мебели; габариты — по паспортам изделий.
5. Двери скрытого монтажа — полотно в плоскости стены, отделка стены по полотну, плинтус прерывается у короба (узел — на листе узлов).

1000 мм · печать 1:1

**Допущения и предложения на листе**

Основа листа: размеры сняты со скана обмерного плана KV оформление (см): часть подписей не читается, помещения выровнены по читаемым размерам; контрольный обмер не выполнен (К-1); высота потолка 2650 мм принята по отметкам обмера (Н = 2,50…2,66 м, ригель 2,28 м) — уточнить при обмере (К-2); толщины стен 300 / 120 мм приняты, межквартирная стена и колонны — по скану, не замерены (К-1); разрешённая мощность 15 кВт принята по типовым ТУ; при объединении двух квартир — переоформление ТУ (К-4); подрайон климата не задан — принят не северный (жилые от 2,5 м) (К-8).

Знак «*» — принято, не замерено и не подтверждено (замерить на объекте): К-1: окно пом. 10 (стена Б) — Окно 1300 при смещение 3500 на стене Б основной части (длина 3830) выходило за стену на 970 мм.

См. лист открытых вопросов (лист 6, записи К-1, К-2, К-4, К-8).

| Изм. | Кол.уч | Лист | № док. | Подп. | Дата |
|---|---|---|---|---|---|
| Разраб. | | Кырлан А.С. | | | 04.11.26 |
| Пров. | | | | | |
| ГИП | | | | | |
| | | | | | |
| Н. контр. | | | | | |
| Утв. | | | | | |

**ГД-2026-009-АИ**

Квартира 103 м²

Общая площадь 100,72* м² · * размеры со скана, не замерены (реестр — л. 6, 7, К-1)

| Дизайн-проект интерьера | Стадия | Лист | Листов |
|---|---|---|---|
| | РП | 108 | 120 |

**Развёртки стен В, Г1. Спальня мастер (пом. 10)**

М 1:25

**Кырлан Александр Сергеевич**


выпуск 04.11.2026 № 35b47f1c2a · стр. 117 из 130

# Развёртка стены Г2. Спальня мастер (пом. 10)


Спальня мастер (пом. 10) · вид изнутри помещения · размеры в мм, отметки в м

**ПРЕДВАРИТЕЛЬНО · не для производства работ · открыто пунктов: 8 (реестр — л. 6, 7)**

## Развёртка стены Г2

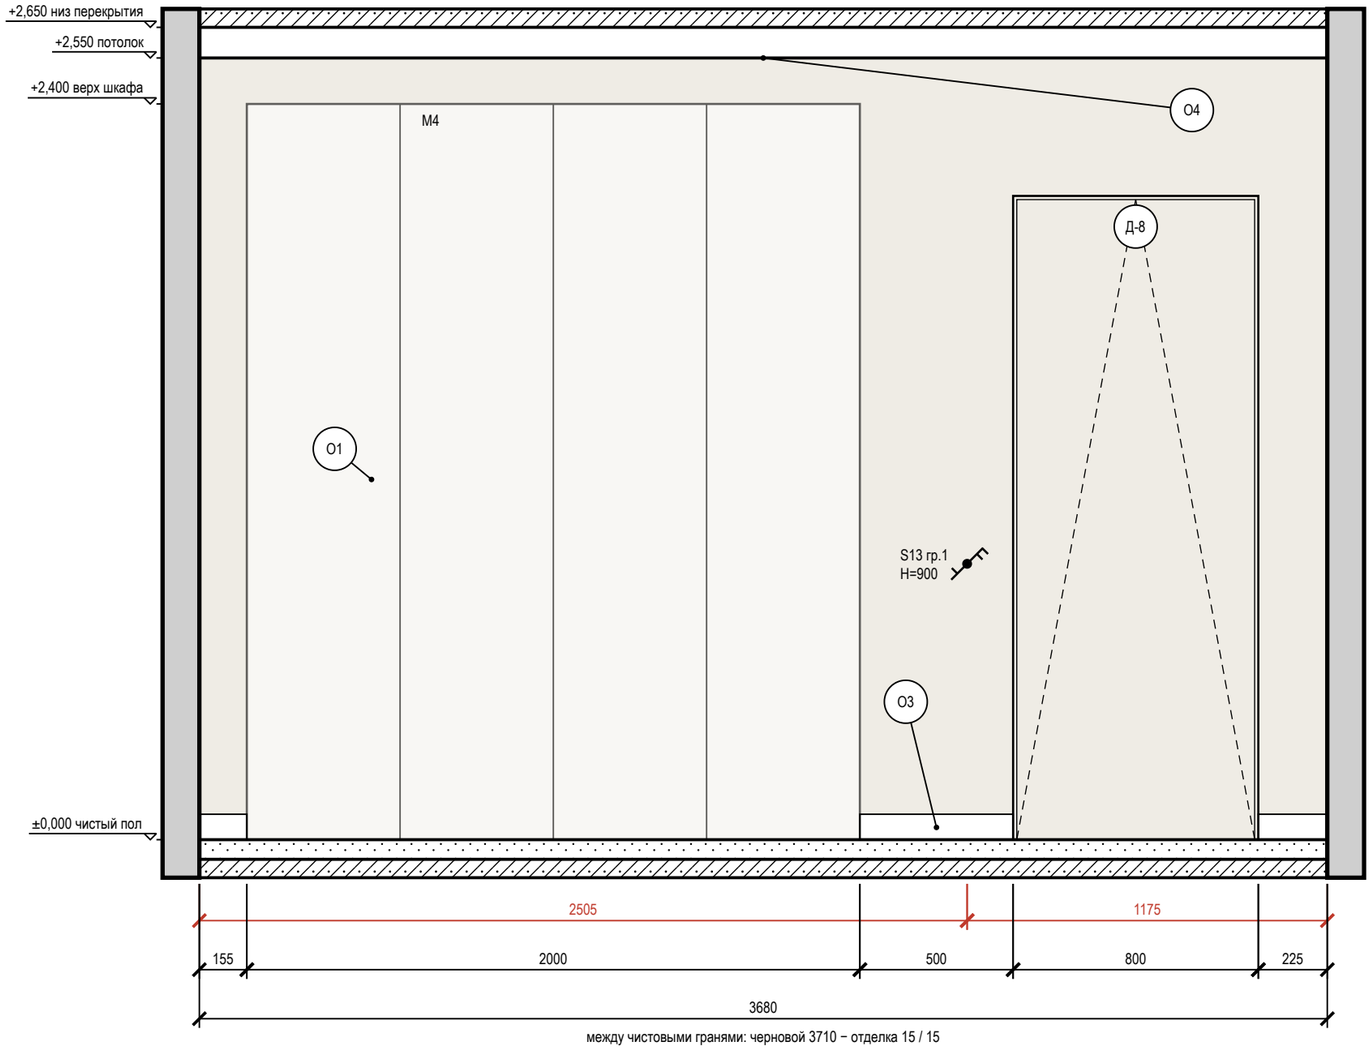


## Схема развёрток (М 1:100)

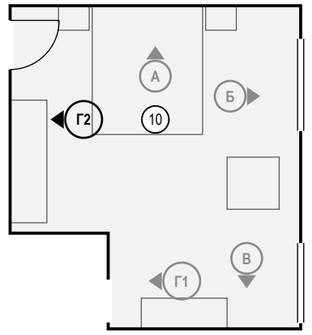


## Условные обозначения

- выключатель одноклавишный
- выключатель двухклавишный (флажков — по числу клавиш)
- выключатель с проходной или перекрёстной клавишей (обратный флажок); тип клавиши — в подписи
- привязки точек и выводов от угла и от пола, мм
- мебель и приборы — фасад по расстановке (условно)
- дверь скрытого монтажа: полотно в плоскости стены (узел — на листе узлов)
- стены и перекрытия в сечении
- окраска: тон — цвет по коду производителя (условно)
- О1 — марка отделки по реестру отделки альбома
- А — марка развёртки: буква стены, стрелка — взгляд

## Ведомость отделки (на листе)

| Марка | Поверхность | Материал, изделие | Цвет, код | Кол. |
|---|---|---|---|---|
| О1 | стены | окраска, Farrow & Ball Modern Emulsion, матовая, подготовка Q3 | Farrow & Ball No. 291 «School House White — тёплый меловой белый» | 7,7 м² |
| О3 | плинтус | плинтус МДФ, h 83 мм, Ultrawood Base 5340, ЛДФ под окраску, 83×15 мм, 2440 мм (арт. LDF-BASE-5340) | Farrow & Ball No. 291 «School House White — тёплый меловой белый» | 0,9 м |
| О4 | потолок | окраска, Tikkurila Anti-Reflex 2, глубокоматовая, подготовка Q3 | NCS S 0502-Y «Белый с лёгкой желтизной» | 22,5 м² |

**Допущения и предложения на листе**

Основа листа: размеры сняты со скана обмерного плана KV оформление (см): часть подписей не читается, помещения выровнены по читаемым размерам; контрольный обмер не выполнен (К-1); высота потолка 2650 мм принята по отметкам обмера (Н = 2,50…2,66 м, ригель 2,28 м) — уточнить при обмере (К-2); толщины стен 300 / 120 мм приняты, межквартирная стена и колонны — по скану, не замерены (К-1); разрешённая мощность 15 кВт принята по типовым ТУ; при объединении двух квартир — переоформление ТУ (К-4); подрайон климата не задан — принят не северный (жилые от 2,5 м) (К-8).

Знак «*» — принято, не замерено и не подтверждено (замерить на объекте): К-1: окно пом. 10 (стена Б) — Окно 1300 при смещение 3500 на стене Б основной части (длина 3830) выходило за стену на 970 мм.

См. лист открытых вопросов (лист 6, записи К-1, К-2, К-4, К-8).

## Примечания

1. Развёртки — вид на стену изнутри помещения, по часовой стрелке; расположение — на схеме листа и на листе 79; размеры — в мм по чистовым поверхностям; отметки — в м от ±0,000; высоты Н — от чистого пола помещения до оси изделия, у декора — до центра.
2. Красная цепочка — привязки электроточек и выводов по осям от угла чистовых стен; высота Н — у знака, от чистого пола до оси; высоты мебели, проёмов и границ отделки — колонкой отметок слева. Стена с 5 и более точками или с мелкими звеньями привязок показана двумя видами: архитектурная развёртка (мебель, отделка, проёмы, высоты) и вид «Привязки» на отдельном листе — точки и выводы с марками, одна цепочка по осям и таблица привязок (каждая точка — строка).
3. У знака электроточки: марка (Р — розетка, S — выключатель, Св — светильник, ЭВ — вывод кабеля), ×N — число постов в рамке, гр. — группа щита, Н — высота оси от чистого пола, мм; группы по клавишам выключателя — на листе выключателей.
4. Схема мебели, приборов и декора не является технической документацией для производства мебели; габариты — по паспортам изделий.
5. Двери скрытого монтажа — полотно в плоскости стены, отделка стены по полотну, плинтус прерывается у короба (узел — на листе узлов).

1000 мм · печать 1:1

| Изм. | Кол.уч | Лист | № док. | Подп. | Дата |
|---|---|---|---|---|---|
| Разраб. | | Кырлан А.С. | | | 04.11.26 |
| Пров. | | | | | |
| ГИП | | | | | |
| Н. контр. | | | | | |
| Утв. | | | | | |

**ГД-2026-009-АИ**

Квартира 103 м²

Общая площадь 100,72* м² · * размеры со скана, не замерены (реестр — л. 6, 7, К-1)

Дизайн-проект интерьера

| Стадия | Лист | Листов |
|---|---|---|
| РП | 109 | 120 |

**Развёртка стены Г2. Спальня мастер (пом. 10)**

М 1:20

**Кырлан Александр Сергеевич**


выпуск 04.11.2026 № 35b47f1c2a · стр. 118 из 130

# Развёртки стен А, Б, В. Ванная мастер (пом. 11)

Ванная мастер (пом. 11) · вид изнутри помещения · размеры в мм, отметки в м


**ПРЕДВАРИТЕЛЬНО · не для производства работ · открыто пунктов: 8 (реестр — л. 6, 7)**

## Развёртка стены А

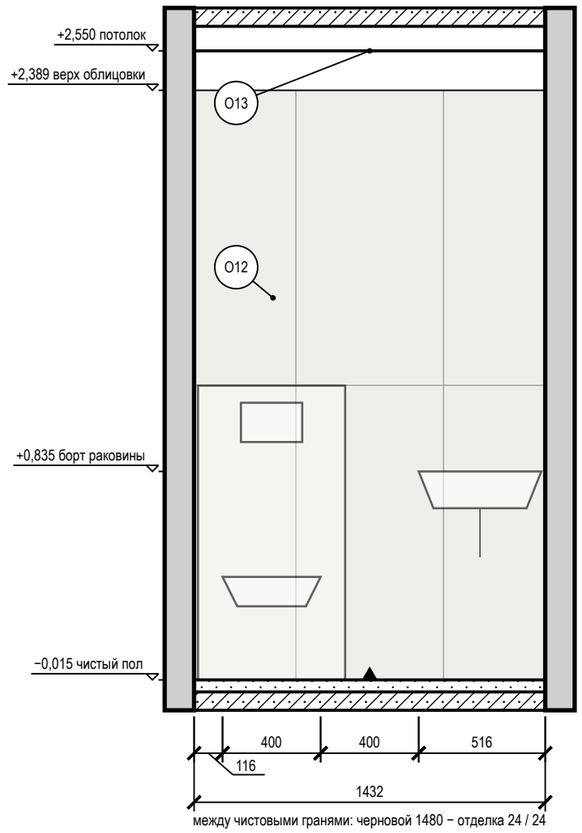



между чистовыми гранями: черновой 1480 − отделка 24 / 24

## Развёртка стены Б

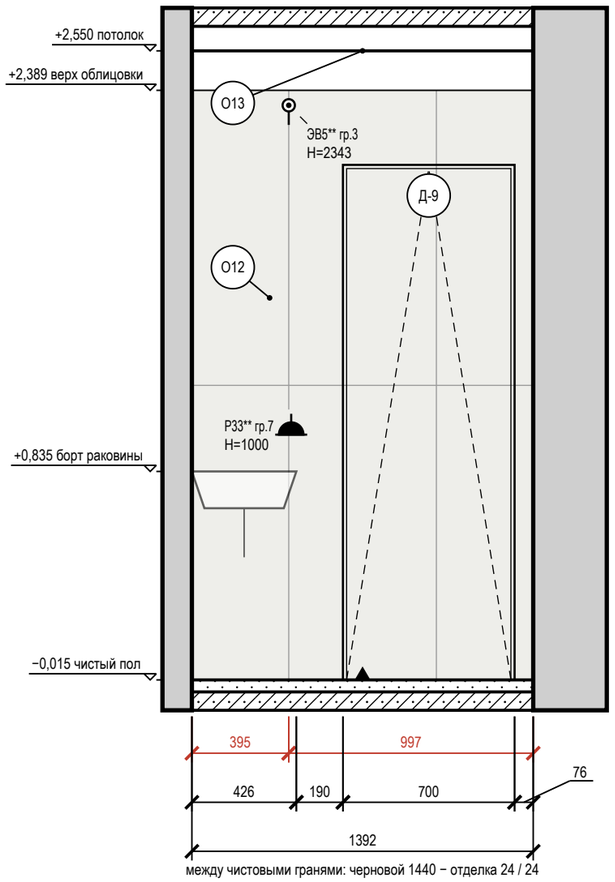



между чистовыми гранями: черновой 1440 − отделка 24 / 24

## Развёртка стены В

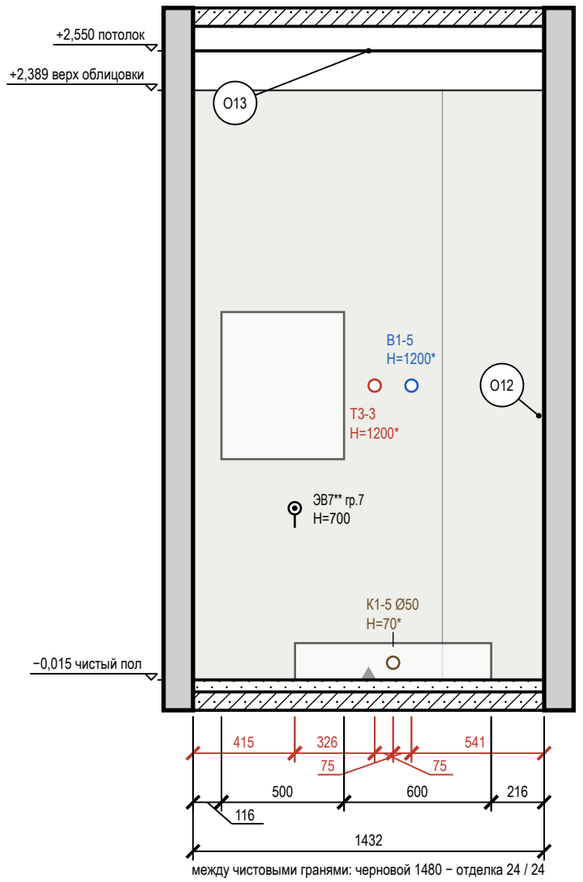


между чистовыми гранями: черновой 1480 − отделка 24 / 24

## Схема развёрток (М 1:100)

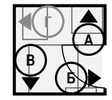


**Допущения и предложения на листе**

Основа листа: размеры сняты со скана обмерного плана KV оформление (см): часть подписей не читается, помещения выровнены по читаемым размерам; контрольный обмер не выполнен (К-1); высота потолка 2650 мм принята по отметкам обмера (Н = 2,50…2,66 м, ригель 2,28 м) — уточнить при обмере (К-2); толщины стен 300 / 120 мм приняты, межквартирная стена и колонны — по скану, не замерены (К-1); разрешённая мощность 15 кВт принята по типовым ТУ; при объединении двух квартир — переоформление ТУ (К-4); подрайон климата не задан — принят не северный (жилые от 2,5 м) (К-8).

Знак «**» — предложение проектировщика, заказчиком не утверждено (согласовать с заказчиком): ЭВ5 — по образцу: Добавлены выводы к вентиляторам: ЭВ4 (ВР1, ванная) и ЭВ5 (ВР3, санузел 2) — группа 3, высота 2389 мм, включение с основным светом, таймер выбега в вентиляторе; и коробки уравнивания потенциалов КУП1 (ванная) и КУП2 (санузел 2) — высота 300 мм, у входа, вне зон 0–2, проводник от шины PE щита ЩК …; сдвиг под раскладку плитки стены Б на 29 мм вдоль стены и на 46 мм ниже — ось на шве или в центре плитки, привязка по таблице листа; ИЗ-1: Р33 — по образцу: Розетка Р33 на высоте 1100 мм, вне шва плитки; ЭВ7 — по образцу: Добавлены электрические полотенцесушители IP44: П10 в ванной (480 мм, низ 900 мм) и П13 в санузле 2 (400 мм, низ 900 мм), выводы ЭВ6 и ЭВ7; мощность группы 13 — 2,4 кВт вместо 1,8 кВт; сдвиг под раскладку плитки стены В на 101 мм вдоль стены — ось на шве или в центре плитки, привязка по таблице листа.

См. лист открытых вопросов (лист 6, записи ИЗ-1, К-1, К-2, К-4, К-8).

## Условные обозначения

- розетка влагозащищённая IP44
- вывод кабеля для подключения прибора (без розетки), марка ЭВ
- вывод В1 (код — в ведомости привязок)
- вывод Т3 (код — в ведомости привязок)
- вывод К1 (код — в ведомости привязок)
- привязки точек и выводов от угла и от пола, мм
- мебель и приборы — фасад по расстановке (условно)
- дверь скрытого монтажа: полотно в плоскости стены (узел — на листе узлов)
- стены и перекрытия в сечении
- плитка: сетка швов по формату, ▲ — ось старта
- О1 — марка отделки по реестру отделки альбома
- А — марка развёртки: буква стены, стрелка — взгляд

## Примечания

1. Развёртки — вид на стену изнутри помещения, по часовой стрелке; расположение — на схеме листа и на листе 79; размеры — в мм по чистовым поверхностям; отметки — в м от ±0,000; высоты Н — от чистого пола помещения до оси изделия, у декора — до центра.
2. Красная цепочка — привязки электроточек и выводов по осям от угла чистовых стен; высота Н — у знака, от чистого пола до оси; высоты мебели, проёмов и границ отделки — колонкой отметок слева. Стена с 5 и более точками или с мелкими звеньями привязок показана двумя видами: архитектурная развёртка (мебель, отделка, проёмы, высоты) и вид «Привязки» на отдельном листе — точки и выводы с марками, одна цепочка по осям и таблица привязок (каждая точка — строка).
3. Стена А показана двумя видами: здесь — архитектурная развёртка (мебель, отделка, проёмы, высоты), электроточки и выводы ВК с привязками и таблицей — на листе 111 («Привязки»).
4. У знака электроточки: марка (Р — розетка, S — выключатель, Св — светильник, ЭВ — вывод кабеля), ×N — число постов в рамке, гр. — группа щита, Н — высота оси от чистого пола, мм; группы по клавишам выключателя — на листе выключателей.
5. Схема мебели, приборов и декора не является технической документацией для производства мебели; габариты — по паспортам изделий (* — высота не задана в проекте, показана по типовому изделию).
6. Выводы ВК — коды и высоты по листу выводов сантехники; * — высота принята по типовой практике монтажа, окончательно — по паспорту прибора.
7. Облицовка — по сетке швов 2 мм, раскладка от оси стены (треугольник у пола), целые ряды от пола; подрезки — по листу раскладки плитки.
8. Гидроизоляция в 2 слоя, заход на стены 200 мм; у душа — до 2000 и 500 мм за поддон — до облицовки, с актом скрытых работ и тестом проливом (узел — на листе узлов).
9. Двери скрытого монтажа — полотно в плоскости стены, отделка стены по полотну, плинтус прерывается у короба (узел — на листе узлов).
10. Линии узора (швы плитки, складки штор, рёбра радиаторов) прерываются у знаков и выносок — просвет между линиями не менее 0,7 мм.

1000 мм · печать 1:1

## Ведомость отделки (на листе)

| Марка | Поверхность | Материал, изделие | Цвет, код | Кол. |
|---|---|---|---|---|
| О12 | стены | облицовка плиткой, Atlas Concorde Marvel Travertine, 600×1200×9 мм, A8UZ, затирка CG2WA | Atlas Concorde A8UZ «Marvel Travertine» | 8,8 м² |
| О13 | потолок | окраска, Tikkurila Luja 7, матовая, подготовка Q3 | NCS S 0502-Y «Белый с лёгкой желтизной» | 2,1 м² |

| Изм. | Кол.уч | Лист | № док. | Подп. | Дата |
|---|---|---|---|---|---|
| Разраб. | | Кырлан А.С. | | | 04.11.26 |
| Пров. | | | | | |
| ГИП | | | | | |
| | | | | | |
| Н. контр. | | | | | |
| Утв. | | | | | |

**ГД-2026-009-АИ**

Квартира 103 м²

Общая площадь 100,72* м² · * размеры со скана, не замерены (реестр — л. 6, 7, К-1)

Дизайн-проект интерьера

| Стадия | Лист | Листов |
|---|---|---|
| РП | 110 | 120 |

**Развёртки стен А, Б, В. Ванная мастер (пом. 11)**

М 1:25

**Кырлан Александр Сергеевич**


выпуск 04.11.2026 № 35b47f1c2a · стр. 119 из 130

# Привязки электроточек и выводов ВК, стена А. Ванная мастер (пом. 11)

Ванная мастер (пом. 11) · вид изнутри помещения · привязки в мм, отметки в м · к развёртке на листе 110

**ПРЕДВАРИТЕЛЬНО · не для производства работ · открыто пунктов: 8 (реестр — л. 6, 7)**

### Развёртка стены А: электроточки и выводы

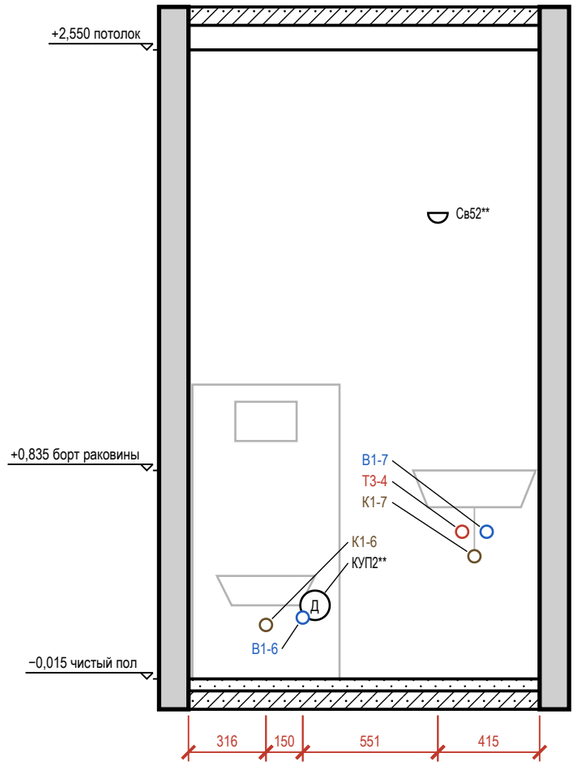



### Таблица привязок электроточек и выводов

| Марка | Назначение | От угла, мм | Н от пола, мм | Примечание |
|---|---|---|---|---|
| К1-6 | канализация — унитаз подвесной | 316 | 220* | Ø110 |
| В1-6 | холодная вода — унитаз подвесной | 466 | 250* | в раме инсталляции |
| КУП2** | КУП — уравнивание потенциалов (ДСУП) | 516 | 300 | |
| Св52** | светильник настенный | 1017 | 1900 | гр. 3 |
| Т3-4 | горячая вода — умывальник | 1116 | 600* | межос. 100 |
| К1-7 | канализация — умывальник | 1166 | 500* | Ø50 |
| В1-7 | холодная вода — умывальник | 1216 | 600* | межос. 100 |

### Условные обозначения

- светильник настенный (бра), Н — высота оси
- вывод В1 (код — в ведомости привязок)
- вывод Т3 (код — в ведомости привязок)
- вывод К1 (код — в ведомости привязок)
- привязки точек и выводов от угла и от пола, мм
- марка развёртки: буква стены, стрелка — взгляд

### Схема развёрток (М 1:50)

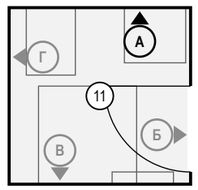


### Примечания

1. Вид «Привязки» стены А — электроточки и выводы ВК; архитектурная развёртка (мебель, отделка, проёмы, высоты) — на листе 110, расположение — на листе 79. Мебель и приборы — подложкой для ориентира; их марки и обозначения мебели, проёмов и стен — там же.
2. Привязки — в мм: по горизонтали от левого чистового угла стены до оси изделия, Н — от чистого пола до оси; все точки — в таблице привязок. Красная цепочка — привязки по осям; точки ближе 150 мм одна к другой в цепочку не дробятся — их привязки только в таблице.
3. У знака — марка электроточки (Р — розетка, S — выключатель, Св — светильник, ЭВ — вывод кабеля); посты в рамке и группа щита — в графе «Примечание»; группы по клавишам выключателя — на листе выключателей.
4. Коды выводов ВК: В1 — холодная вода, Т3 — горячая вода, К1 — канализация; номер после дефиса — номер вывода на листе выводов сантехники; * — высота принята по типовой практике монтажа, окончательно — по паспорту прибора.

**Допущения и предложения на листе**

Основа листа: размеры сняты со скана обмерного плана KV оформление (см): часть подписей не читается, помещения выровнены по читаемым размерам; контрольный обмер не выполнен (К-1); высота потолка 2650 мм принята по отметкам обмера (Н = 2,50…2,66 м, ригель 2,28 м) — уточнить при обмере (К-2); толщины стен 300 / 120 мм приняты, межквартирная стена и колонны — по скану, не замерены (К-1); разрешённая мощность 15 кВт принята по типовым ТУ; при объединении двух квартир — переоформление ТУ (К-4); подрайон климата не задан — принят не северный (жилые от 2,5 м) (К-8).

Знак «**» — предложение проектировщика, заказчиком не утверждено (согласовать с заказчиком): Св52 — свет у зеркала — над зеркалом у умывальника по его оси (свет на лицо, а не над сантехникой); сдвиг под раскладку плитки стены А на 149 мм вдоль стены — ось на шве или в центре плитки, привязка по таблице листа; КУП2 — по образцу: Добавлены выводы к вентиляторам: ЭВ4 (ВР1, ванная) и ЭВ5 (ВР3, санузел 2) — группа 3, высота 2389 мм, включение с основным светом, таймер выбега в вентиляторе; и коробки уравнивания потенциалов КУП1 (ванная) и КУП2 (санузел 2) — высота 300 мм, у входа, вне зон 0–2, проводник от шины PE щита ЩК ….

См. лист открытых вопросов (лист 6, записи К-1, К-2, К-4, К-8).

1000 мм · печать 1:1

| Изм. | Кол.уч | Лист | № док. | Подп. | Дата |
|---|---|---|---|---|---|
| Разраб. | | Кырлан А.С. | | | 04.11.26 |
| Пров. | | | | | |
| ГИП | | | | | |
| | | | | | |
| Н. контр. | | | | | |
| Утв. | | | | | |

**ГД-2026-009-АИ**

Квартира 103 м²

Общая площадь 100,72* м² · * размеры со скана, не замерены (реестр — л. 6, 7, К-1)

| Дизайн-проект интерьера | Стадия | Лист | Листов |
|---|---|---|---|
| | РП | 111 | 120 |

**Привязки электроточек и выводов ВК, стена А.**
**Ванная мастер (пом. 11)**
М 1:25

**Кырлан Александр Сергеевич**


выпуск 04.11.2026 № 35b47f1c2a · стр. 120 из 130

# Развёртка стены Г. Ванная мастер (пом. 11)

Ванная мастер (пом. 11) · вид изнутри помещения · размеры в мм, отметки в м

**ПРЕДВАРИТЕЛЬНО · не для производства работ · открыто пунктов: 8 (реестр — л. 6, 7)**

## Развёртка стены Г

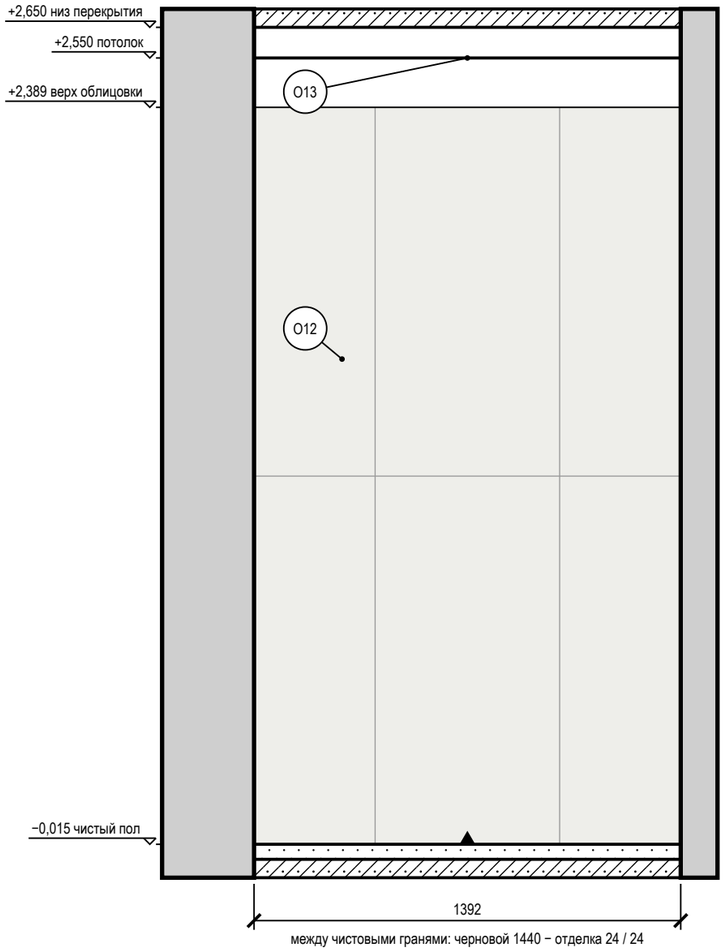


## Схема развёрток (М 1:100)




## Условные обозначения

- мебель и приборы — фасад по расстановке (условно)
- стены и перекрытия в сечении
- плитка: сетка швов по формату, ▲ — ось старта
- О1 — марка отделки по реестру отделки альбома
- А — марка развёртки: буква стены, стрелка — взгляд

## Ведомость отделки (на листе)

| Марка | Поверхность | Материал, изделие | Цвет, код | Кол. |
|---|---|---|---|---|
| О12 | стены | облицовка плиткой, Atlas Concorde Marvel Travertine, 600×1200×9 мм, A8UZ, затирка CG2WA | Atlas Concorde A8UZ «Marvel Travertine» | 3,3 м² |
| О13 | потолок | окраска, Tikkurila Luja 7, матовая, подготовка Q3 | NCS S 0502-Y «Белый с лёгкой желтизной» | 2,1 м² |

## Примечания

1. Развёртки — вид на стену изнутри помещения, по часовой стрелке; расположение — на схеме листа и на листе 79; размеры — в мм по чистовым поверхностям; отметки — в м от ±0,000; высоты Н — от чистого пола помещения до оси изделия, у декора — до центра.
2. Схема мебели, приборов и декора не является технической документацией для производства мебели; габариты — по паспортам изделий.
3. Облицовка — по сетке швов 2 мм, раскладка от оси стены (треугольник у пола), целые ряды от пола; подрезки — по листу раскладки плитки.
4. Гидроизоляция в 2 слоя, заход на стены 200 мм; у душа — до 2000 и 500 мм за поддон — до облицовки, с актом скрытых работ и тестом проливом (узел — на листе узлов).

**Допущения и предложения на листе**

Основа листа: размеры сняты со скана обмерного плана KV оформление (см): часть подписей не читается, помещения выровнены по читаемым размерам; контрольный обмер не выполнен (К-1); высота потолка 2650 мм принята по отметкам обмера (Н = 2,50…2,66 м, ригель 2,28 м) — уточнить при обмере (К-2); толщины стен 300 / 120 мм приняты, межквартирная стена и колонны — по скану, не замерены (К-1); разрешённая мощность 15 кВт принята по типовым ТУ; при объединении двух квартир — переоформление ТУ (К-4); подрайон климата не задан — принят не северный (жилые от 2,5 м) (К-8).
См. лист открытых вопросов (лист 6, записи К-1, К-2, К-4, К-8).

1000 мм · печать 1:1

| Изм. | Кол.уч | Лист | № док. | Подп. | Дата |
|---|---|---|---|---|---|
| Разраб. | | Кырлан А.С. | | | 04.11.26 |
| Пров. | | | | | |
| ГИП | | | | | |
| | | | | | |
| Н. контр. | | | | | |
| Утв. | | | | | |

**ГД-2026-009-АИ**

Квартира 103 м²

Общая площадь 100,72* м² · * размеры со скана, не замерены (реестр — л. 6, 7, К-1)

Дизайн-проект интерьера

| Стадия | Лист | Листов |
|---|---|---|
| РП | 112 | 120 |

**Развёртка стены Г. Ванная мастер (пом. 11)**

М 1:20

**Кырлан Александр Сергеевич**


выпуск 04.11.2026 № 35b47f1c2a · стр. 121 из 130

# Узлы

Пороги и стыки покрытий, скрытые двери, короба стояков, гидроизоляция, плинтус


### 1 Порог 15 мм: мокрая зона — смежное помещение (М 1:10)

Применение: двери Д-5, Д-9; места — лист 79

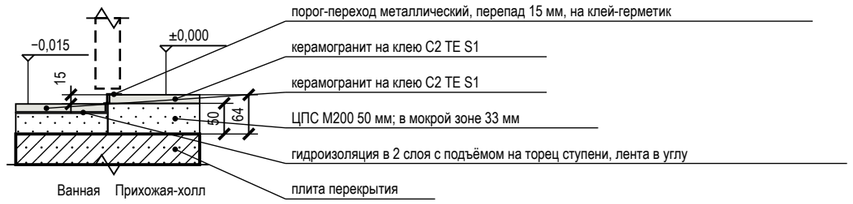



### 2 Дверь скрытого монтажа в плоскости стены, плинтус (М 1:5)

Применение: двери Д-2, Д-3, Д-4, Д-5, Д-6, Д-7, Д-8, Д-9; места — лист 79

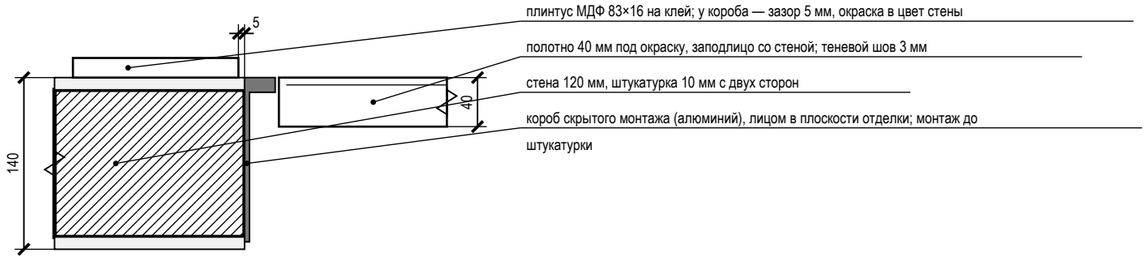



### 3 Короб стояков К1-1, К1-2 (кухня) с люком и звукоизоляцией (М 1:10)

Применение: пом. 6, 5, 11, 7; места — лист 79

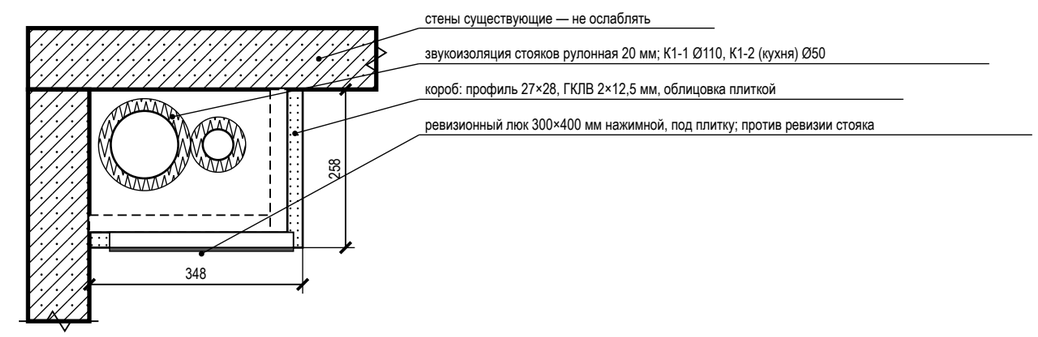



### 4 Гидроизоляция санузла: заход на стены 200 мм, примыкание ванны (М 1:20)

Применение: пом. 6, 11; места — лист 79

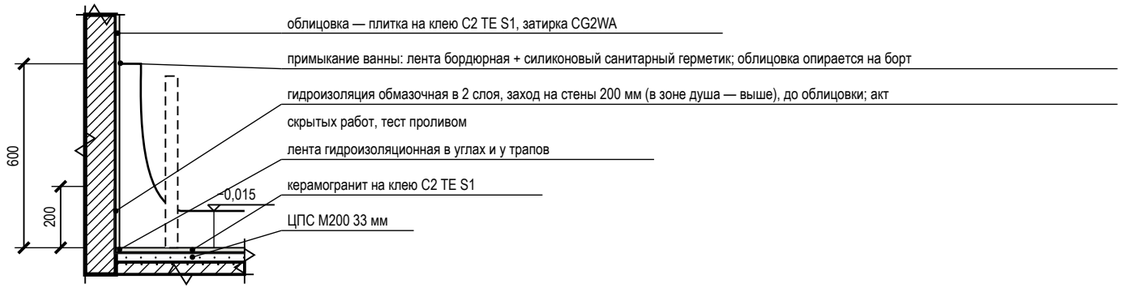



### 5 Плинтус МДФ 83×15 мм у окрашенной стены по доске (ламинату) (М 1:10)

Применение: пом. 1, 2, 3, 5, 7, 8, 9, 10; места — лист 79

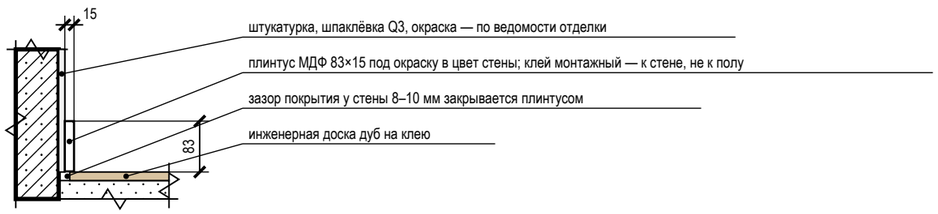


### 6 Плинтус МДФ 83×15 мм у окрашенной стены по керамограниту (плитке) (М 1:10)

Применение: пом. 4; места — лист 79

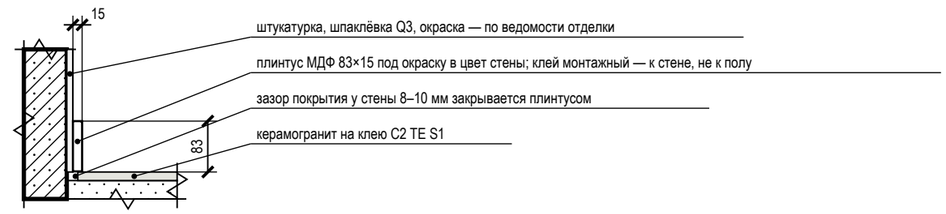


## Условные обозначения

- железобетон (плита, стены) — условно: конструкция не установлена
- кладка, перегородка — условно: конструкция не установлена
- стяжка, раствор
- гипсокартон ГКЛВ
- звукоизоляция, эластичный заполнитель
- плитка, керамогранит на клею
- инженерная доска (покрытие пола)
- металлический профиль (порог, Т-профиль, короб двери)
- гидроизоляция (обмазочная, лента)

## Примечания

1. Узлы — типовые решения проекта для мест, отмеченных выносками на листе схемы расположения развёрток и узлов; размеры — в мм, отметки — в м от ±0,000.
2. Узлы с гидроизоляцией, закладными и коробами скрытого монтажа принимаются по актам скрытых работ до закрытия отделкой; гидроизоляция — после теста проливом (24 ч).
3. Марки изделий (порог, Т-профиль, короб скрытой двери, люк) — по спецификациям; замена — на аналог с теми же габаритами по согласованию с автором проекта.
4. Материал плиты перекрытия и стен в узлах показан условно (железобетон, кладка): конструкция дома не установлена — крепёж, анкеры и толщины слоёв уточняются после обследования (до него — по допущениям общих указаний).

Допущения и предложения на листе. Основа листа: размеры сняты со скана обмерного плана KV оформление (см): часть подписей не читается, помещения выровнены по читаемым размерам; контрольный обмер не выполнен (К-1); высота потолка 2650 мм принята по отметкам обмера (Н = 2,50…2,66 м, ригель 2,28 м) — уточнить при обмере (К-2); толщины стен 300 / 120 мм приняты, межквартирная стена и колонны — по скану, не замерены (К-1); разрешённая мощность 15 кВт принята по типовым ТУ; при объединении двух квартир — переоформление ТУ (К-4); подрайон климата не задан — принят не северный (жилые от 2,5 м) (К-8). См. лист открытых вопросов (лист 6, записи К-1, К-2, К-4, К-8).

| Изм. | Кол.уч | Лист | № док. | Подп. | Дата |
|---|---|---|---|---|---|
| Разраб. | | Кырлан А.С. | | | 04.11.26 |
| Пров. | | | | | |
| ГИП | | | | | |
| Н. контр. | | | | | |
| Утв. | | | | | |

**ГД-2026-009-АИ**

Квартира 103 м²

Общая площадь 100,72* м² · * размеры со скана, не замерены (реестр — л. 6, 7, К-1)

Дизайн-проект интерьера

| Стадия | Лист | Листов |
|---|---|---|
| РП | 113 | 120 |

**Узлы**

М 1:10; 1:5; 1:20

**Кырлан Александр Сергеевич**

выпуск 04.11.2026 № 35b47f1c2a · стр. 122 из 130

10

# Смета

Кырлан Александр Сергеевич

выпуск 04.11.2026 № 35b47f1c2a · стр. 123 из 130

# Ведомость объёмов работ

**ПРЕДВАРИТЕЛЬНО · не для производства работ · открыто пунктов: 8 (реестр — л. 6, 7)**

Объёмы по помещениям от чертежа · площади в м², длины в м · формула, правило проёмов и источник в каждой строке

## Ведомость объёмов работ по помещениям

| Поз. | Наименование работ (материал, число слоёв) | Ед. изм. | Объём по помещениям (№ по экспликации) | | | | | | | | | | | Всего | Формула подсчёта | Правило проёмов | Источник | Цена за ед., ₽ | Стоимость, ₽ |
|---|---|---|---|---|---|---|---|---|---|---|---|---|---|---|---|---|---|---|---|
| | | | 1 | 2 | 3 | 4 | 5 | 6 | 7 | 8 | 9 | 10 | 11 | | | | | | |
| **1. Демонтаж и черновые работы** | | | | | | | | | | | | | | | | | | | |
| 1 | Демонтаж существующего покрытия пола до основания | м² | 10,57 | 2,93 | 20,32 | 12,91 | 6,52 | 3,91 | 1,51 | 11,42 | 6,02 | 22,48 | 2,13 | 100,72 | S пом. | | л. 14, 15 | по КП | |
| 2 | Демонтаж существующей отделки стен до основания | м² | 31,33 | 17,61 | 35,31 | 33,88 | 22,52 | 19,31 | 11,89 | 32,98 | 29,17 | 43,57 | 13,51 | 291,08 | P × H − проёмы | за вычетом проёмов | л. 14, 15 | по КП | |
| 3 | Демонтаж существующей отделки потолка до основания | м² | 10,57 | 2,93 | 20,32 | 12,91 | 6,52 | 3,91 | 1,51 | 11,42 | 6,02 | 22,48 | 2,13 | 100,72 | S пом. | | л. 14, 15 | по КП | |
| 4 | Демонтаж существующих дверных блоков | шт | 1 | 1 | | 1 | 1 | 1 | 1 | 1 | | 1 | 1 | 9 | по ведомости проёмов | | л. 15–17 | по КП | |
| 5 | Демонтаж существующих сантехприборов и электрооборудования (если есть) | компл | | | | | | | | | | | | | по факту на объекте | | л. 15 | по КП | |
| 6 | Устройство стяжки: стяжка ЦПС М200, 50 мм | м² | 10,62 | 2,97 | 20,55 | 13,22 | 6,57 | 3,95 | 1,55 | 11,46 | 6,22 | 22,57 | 2,17 | 101,85 | S пом. + S в дверных проёмах (b × t/2) | проёмы добавлены | л. 53–56 | 530 | 53 981 |
| 7 | Гидроизоляция обмазочная, 2 слоя: пол, стены на 200 мм, зоны замачивания | м² | | | | | | 11,45 | | | | | 5,56 | 17,01 | пол + (P − двери) × h заведения + зоны замачивания | | л. 49 | 450 | 7 655 |
| 8 | Штукатурка стен по маякам, до 10 мм | м² | 31,33 | 17,61 | 35,31 | 33,88 | 22,52 | 19,31 | 11,89 | 32,98 | 29,17 | 43,57 | 13,51 | 291,08 | P × H − проёмы по обводу коробок − грани перегородок на ГКЛВ | за вычетом проёмов | л. 14, 54–56 | 530 | 154 272 |
| 9 | Штукатурка оконных откосов шириной более 200 мм | м² | 0,99 | | 2,02 | | 0,99 | | | 1,01 | | 2,07 | | 7,08 | Σ (2h + b) × глубина откоса | откосы > 200 мм | л. 14 | 540 | 3 823 |
| 10 | Потолок ГКЛ по каркасу П113, 1 слой | м² | 10,57 | | 20,32 | 12,91 | 6,52 | 3,91 | | 11,42 | 6,02 | 22,48 | 2,13 | 96,28 | S пом. по плану потолков | | л. 45–48 | 1 500 | 144 420 |
| **Итого по разделу 1 — 364 151 ₽ (позиций 10, из них по КП 5); в сводную смету — л. 119, 120** | | | | | | | | | | | | | | | | | | | |
| **2. Инженерные системы** | | | | | | | | | | | | | | | | | | | |
| 11 | Прокладка кабеля ВВГнг(A)-LS по группам щита: за потолком и в штробах стен (штробы — только после технического заключения, см. строку «Штробы в стенах») | м | | | | | | | | | | | | 595,50 | Σ длин групп щита | | л. 28 | 60 | 35 730 |
| 12 | Прокладка слаботочной линии: Кабель домофона — тип по системе поставщика, отдельно от силовых | м | | | | | | | | | | | | 4,30 | по лучам от ЩС**: 1 точ., запас 10 % | | л. 30 | по КП | |
| 13 | Прокладка слаботочной линии: Кабель коаксиальный RG-6 (75 Ом) к розеткам ТВ, отдельно от силовых | м | | | | | | | | | | | | 16,10 | по лучам от ЩС**: 1 точ., запас 10 % | | л. 30 | по КП | |
| 14 | Прокладка слаботочной линии: Кабель U/UTP кат. 6 (LAN, Wi-Fi и камеры по PoE), отдельно от силовых | м | | | | | | | | | | | | 70,30 | по лучам от ЩС**: 5 точ., запас 10 % | | л. 30 | по КП | |
| 15 | Прокладка гофротрубы Ø20 для слаботочных линий, отдельно от силовых | м | | | | | | | | | | | | 81,60 | по длине лучей без участков в канале плинтуса (≈ 90 %) | | л. 30 | по КП | |
| 16 | Сборка слаботочного щита ЩС**: корпус, патч-панель, подключение линий и питания 220 В; коммутатор и точки доступа — оборудование заказчика | шт | | | | | | | | | | | | 1 | один щит | | л. 26, 27, 30 | по КП | |
| 17 | Электроточка: подрозетник в бетоне, розетка, выключатель, вывод | шт | 6 | 1 | 10 | 8 | 10 | 3 | 2 | 8 | 2 | 9 | 3 | 62 | по ведомости электроточек | | л. 23, 26, 27 | 950 | 58 900 |
| 18 | Штробы в стенах под спуски кабеля к точкам — выполняются только после технического заключения о несущих стенах | м | 8,40 | 1,75 | 18,40 | 11,35 | 15,70 | 3,59 | 3,40 | 16,00 | 3,90 | 17,45 | 3,65 | 103,59 | Σ (H − h) по точкам на стенах: вертикальные спуски | после техзаключения | л. 15, 23 | по КП | |
| 19 | Установка встраиваемого точечного светильника | шт | 6 | | 8 | 4 | 7 | 3 | | 6 | 2 | 8 | 2 | 46 | по плану освещения | | л. 24 | 750 | 34 500 |
| 20 | Монтаж светильника: потолочного, подвесного, настенного | шт | | 1 | 1 | | | 1 | 1 | 1 | | 2 | 1 | 8 | по плану освещения | | л. 24 | 1 200 | 9 600 |
| 21 | Монтаж LED-ленты в алюминиевый профиль | м | 12,30 | | 5,40 | 1,80 | 1,20 | | | 12,30 | | 15,50 | | 48,50 | Σ длин лент по плану освещения | | л. 24 | 230 | 11 155 |
| 22 | Установка блока питания LED в доступном месте (люк, шкаф) | шт | 1 | | 1 | 1 | 1 | | | 1 | | 1 | | 6 | один на LED-группу | | л. 24 | 570 | 3 420 |
| 23 | Установка автономного пожарного извещателя | шт | 1 | | 1 | 1 | 1 | | | 1 | 1 | 1 | | 7 | по плану розеток | | л. 23 | по КП | |

**Допущения и предложения на листе**

Основа листа: размеры сняты со скана обмерного плана KV оформление (см): часть подписей не читается, помещения выровнены по читаемым размерам; контрольный обмер не выполнен (К-1); высота потолка 2650 мм принята по отметкам обмера (H = 2,50…2,66 м, ригель 2,28 м) — уточнить при обмере (К-2); толщины стен 300 / 120 мм приняты, межквартирная стена и колонны — по скану, не замерены (К-1); разрешённая мощность 15 кВт принята по типовым ТУ; при объединении двух квартир — переоформление ТУ (К-4); подрайон климата не задан — принят не северный (жилые от 2,5 м) (К-8).

Знак «**» — предложение проектировщика, заказчиком не утверждено (согласовать с заказчиком): ЩС — щит слаботочный: место и состав.

См. лист открытых вопросов (лист 6, записи К-1, К-2, К-4, К-8).

| Изм. | Кол.уч | Лист | № док. | Подп. | Дата |
|---|---|---|---|---|---|
| Разраб. | | Кырлан А.С. | | | 04.11.26 |
| Пров. | | | | | |
| ГИП | | | | | |
| | | | | | |
| Н. контр. | | | | | |
| Утв. | | | | | |

**ГД-2026-009-АИ**

Квартира 103 м²

Общая площадь 100,72* м² · * размеры со скана, не замерены (реестр — л. 6, 7, К-1)

Дизайн-проект интерьера

| Стадия | Лист | Листов |
|---|---|---|
| РП | 114 | 120 |

**Ведомость объёмов работ**

М б/м

**Кырлан Александр Сергеевич**

# Ведомость объёмов работ (продолжение)

Объёмы по помещениям от чертежа · площади в м², длины в м · формула, правило проёмов и источник в каждой строке

## Ведомость объёмов работ по помещениям (продолжение)

| Поз. | Наименование работ (материал, число слоёв) | Ед. изм. | Объём по помещениям (№ по экспликации) | | | | | | | | | | | Всего | Формула подсчёта | Правило проёмов | Источник | Цена за ед., ₽ | Стоимость, ₽ |
|---|---|---|---|---|---|---|---|---|---|---|---|---|---|---|---|---|---|---|---|
| | | | 1 | 2 | 3 | 4 | 5 | 6 | 7 | 8 | 9 | 10 | 11 | | | | | | |
| 24 | Сборка щита: установка автоматов и АВДТ групп, вводного автомата | шт | | | | | | | | | | | | 15 | группы + вводной автомат | | л. 28 | 230 | 3 450 |
| 25 | Установка вводного УЗО | шт | | | | | | | | | | | | 1 | по однолинейной схеме | | л. 28 | 380 | 380 |
| 26 | Монтаж инсталляции, установка подвесного унитаза и кнопки смыва | шт | | | | | | 1 | | | | | 1 | 2 | по плану выводов | | л. 33, 42 | 10 500 | 21 000 |
| 27 | Короб инсталляции: каркас и обшивка ГКЛВ в 2 слоя, ревизионный доступ к смыву | шт | | | | | | 1 | | | | | 1 | 2 | по плану выводов | | л. 33, 49–52 | по КП | |
| 28 | Короб К1 над чистым полом: каркас и обшивка ГКЛВ под плитку (материалы — в спецификации ВК) | м.п. | | | | | | 3,55 | 0,44 | | | | 3,08 | 7,07 | Σ открытых участков выпусков К1 (профиль листа разводки ВК) | | л. 33, 42 | по КП | |
| 29 | Установка ванны с сифоном | шт | | | | | | 1 | | | | | | 1 | по плану выводов | | л. 33, 42 | 6 000 | 6 000 |
| 30 | Установка умывальника (мойки) с сифоном и смесителем | шт | | | | | | 1 | | | | | 1 | 2 | по плану выводов | | л. 33, 42 | 3 000 | 6 000 |
| 31 | Установка душевого поддона с трапом, ограждения | шт | | | | | | | | | | | 1 | 1 | по плану выводов | | л. 33, 42 | по КП | |
| 32 | Подключение стиральной (посудомоечной) машины к ВК | шт | | | | | | | 1 | | | | | 1 | по плану выводов | | л. 33 | по КП | |
| 33 | Установка радиатора с узлом подключения и терморегулятором | шт | 1 | | 2 | | 1 | | | 1 | | 2 | | 7 | по плану отопления | | л. 32 | по КП | |
| **Итого по разделу 2 — 190 135 ₽ (позиций 23, из них по КП 12); в сводную смету — л. 119, 120** | | | | | | | | | | | | | | | | | | | |
| **3. Чистовые работы** | | | | | | | | | | | | | | | | | | | |
| 34 | Облицовка стен керамогранитом 600×1200 на клею | м² | | | | | | 17,04 | | | | | 11,85 | 28,89 | по раскладке: зона облицовки − место за коробом | за вычетом проёмов | л. 49–52 | 2 500 | 72 225 |
| 35 | Облицовка короба инсталляции (ГКЛВ) керамогранитом: лицо, боковины, полка | м² | | | | | | 1,76 | | | | | 1,47 | 3,23 | по раскладке: лицо, боковины, полка | | л. 49–52 | 2 500 | 8 075 |
| 36 | Укладка керамогранита на пол, 600×1200, на клею | м² | | | | 13,22 | | 3,95 | | | | | 2,17 | 19,34 | S пом. + S в дверных проёмах | проёмы добавлены | л. 49–53 | 1 800 | 34 812 |
| 37 | Затирка швов керамогранита | м² | | | | 12,91 | | 22,71 | | | | | 15,45 | 51,07 | Σ S облицовки и пола из плитки | | л. 49–52 | 150 | 7 661 |
| 38 | Грунтование стен, 2 слоя (под штукатурку и под отделку) | м² | 31,33 | 17,61 | 35,31 | 33,88 | 22,52 | 19,31 | 11,89 | 32,98 | 29,17 | 43,57 | 13,51 | 291,08 | P × H − проёмы | за вычетом проёмов | л. 54–56 | 96 | 27 944 |
| 39 | Шпаклёвка стен под окраску, 2 слоя (старт и финиш), уровень Q3 | м² | 31,33 | 17,61 | 35,31 | 33,88 | 22,52 | | 11,89 | 32,98 | 29,17 | 43,57 | | 258,26 | P × H − проёмы − фартук | за вычетом проёмов | л. 54–56 | 750 | 193 695 |
| 40 | Грунтование и шпаклёвка оконных откосов, 2 слоя | м.п. | 4,32 | | 8,80 | | 4,30 | | | 4,40 | | 8,99 | | 30,81 | Σ (2h + b) по окнам | по окнам | л. 14 | 300 | 9 243 |
| 41 | Грунтование потолка, 2 слоя | м² | 10,57 | 2,93 | 20,32 | 12,91 | 6,52 | 3,91 | 1,51 | 11,42 | 6,02 | 22,48 | 2,13 | 100,72 | S пом. | | л. 54–56 | 96 | 9 669 |
| 42 | Шпаклёвка потолка под окраску, 2 слоя, уровень Q3 | м² | 10,57 | 2,93 | 20,32 | 12,91 | 6,52 | 3,91 | 1,51 | 11,42 | 6,02 | 22,48 | 2,13 | 100,72 | S пом. | | л. 45–48, 54–56 | 950 | 95 684 |
| 43 | Окраска потолка водно-дисперсионной краской, 2 слоя | м² | 10,57 | 2,93 | 20,32 | 12,91 | 6,52 | 3,91 | 1,51 | 11,42 | 6,02 | 22,48 | 2,13 | 100,72 | S пом. | | л. 54–56 | 360 | 36 259 |
| 44 | Окраска стен водно-дисперсионной краской, 2 слоя | м² | 34,88 | 19,08 | 47,53 | 41,57 | 26,06 | | 13,36 | 36,47 | 36,31 | 51,05 | | 306,31 | P × H − фартук, проёмы не вычитаются | без вычета проёмов | л. 54–56 | 300 | 91 893 |
| 45 | Окраска оконных откосов, 2 слоя | м.п. | 4,32 | | 8,80 | | 4,30 | | | 4,40 | | 8,99 | | 30,81 | Σ (2h + b) по окнам | по окнам | л. 14 | 120 | 3 697 |
| 46 | Укладка инженерной доски на клей | м² | 10,62 | 2,97 | 20,55 | | 6,57 | | 1,55 | 11,46 | 6,22 | 22,57 | | 82,51 | S пом. + S в дверных проёмах | проёмы добавлены | л. 53–56 | 1 200 | 99 012 |
| 47 | Установка плинтуса МДФ h=83 мм | м.п. | 12,88 | 6,50 | 14,74 | 12,64 | 9,42 | | 4,34 | 13,60 | 10,84 | 18,52 | | 103,48 | P − ширина дверных проёмов | | л. 54–56 | 450 | 46 566 |
| 48 | Окраска плинтуса в тоне No. 291, 2 слоя | м.п. | 12,88 | 6,50 | 14,74 | 12,64 | 9,42 | | 4,34 | 13,60 | 10,84 | 18,52 | | 103,48 | как плинтус | | л. 54–56 | 300 | 31 044 |
| 49 | Монтаж дверей скрытого монтажа под покраску (поставщик дверей) | шт | 1 | 1 | | | 1 | 1 | 1 | 1 | | 1 | 1 | 8 | по ведомости проёмов | | л. 16, 17 | 5 250 | 42 000 |
| 50 | Входная дверь, поставка с монтажом и откосами | шт | | | | | | | | | | | | 1 | по ведомости проёмов | | л. 16, 17 | по КП | |

**Допущения и предложения на листе**

Основа листа: размеры сняты со скана обмерного плана KV оформление (см): часть подписей не читается, помещения выровнены по читаемым размерам; контрольный обмер не выполнен (К-1); высота потолка 2650 мм принята по отметкам обмера (Н = 2,50…2,66 м, ригель 2,28 м) — уточнить при обмере (К-2); толщины стен 300 / 120 мм приняты, межквартирная стена и колонны — по скану, не замерены (К-1); разрешённая мощность 15 кВт принята по типовым ТУ; при объединении двух квартир — переоформление ТУ (К-4); подрайон климата не задан — принят не северный (жилые от 2,5 м) (К-8).

См. лист открытых вопросов (лист 6, записи К-1, К-2, К-4, К-8).

| Изм. | Кол.уч | Лист | № док. | Подп. | Дата |
|---|---|---|---|---|---|
| Разраб. | | Кырлан А.С. | | | 04.11.26 |
| Пров. | | | | | |
| ГИП | | | | | |
| | | | | | |
| Н. контр. | | | | | |
| Утв. | | | | | |

**ГД-2026-009-АИ**

Квартира 103 м²

Общая площадь 100,72* м² · * размеры со скана, не замерены (реестр — л. 6, 7, К-1)

Дизайн-проект интерьера

| Стадия | Лист | Листов |
|---|---|---|
| РП | 115 | 120 |

**Ведомость объёмов работ (продолжение)**

М б/м

**Кырлан Александр Сергеевич**

# Ведомость объёмов работ (окончание)

Объёмы по помещениям от чертежа · площади в м², длины в м · формула, правило проёмов и источник в каждой строке

## Ведомость объёмов работ по помещениям (продолжение)

| Поз. | Наименование работ (материал, число слоёв) | Ед. изм. | Объём по помещениям (№ по экспликации) | | | | | | | | | | | Всего | Формула подсчёта | Правило проёмов | Источник | Цена за ед., ₽ | Стоимость, ₽ |
|---|---|---|---|---|---|---|---|---|---|---|---|---|---|---|---|---|---|---|---|
| | | | 1 | 2 | 3 | 4 | 5 | 6 | 7 | 8 | 9 | 10 | 11 | | | | | | |
| **Итого по разделу 3 — 809 479 ₽ (позиций 17, из них по КП 1); в сводную смету — л. 119, 120** | | | | | | | | | | | | | | | | | | | |

## Ведомость подсчёта площадей по помещениям

| № | Помещение | S пола, м² | P, м | H, м | P × H, м² | Проёмы, м² | Стены нетто, м² | В дверных проёмах, м² | Плинтус, м | Откосы, м.п. |
|---|---|---|---|---|---|---|---|---|---|---|
| 1 | Кабинет-библиотека | 10,57 | 13,68 | 2,55 | 34,88 | 3,55 | 31,33 | 0,05 | 12,88 | 4,32 |
| 2 | Кладовая | 2,93 | 7,20 | 2,65 | 19,08 | 1,47 | 17,61 | 0,04 | 6,50 | нет |
| 3 | Гостиная-столовая | 20,32 | 18,64 | 2,55 | 47,53 | 12,22 | 35,31 | 0,23 | 14,74 | 8,80 |
| 4 | Прихожая-холл | 12,91 | 16,30 | 2,55 | 41,56 | 7,69 | 33,88 | 0,31 | 12,64 | нет |
| 5 | Кухня | 6,52 | 10,22 | 2,55 | 26,06 | 3,54 | 22,52 | 0,05 | 9,42 | 4,30 |
| 6 | Ванная | 3,91 | 8,10 | 2,56 | 20,78 | 1,47 | 19,31 | 0,04 | нет | нет |
| 7 | Постирочная | 1,51 | 5,04 | 2,65 | 13,36 | 1,47 | 11,89 | 0,04 | 4,34 | нет |
| 8 | Спальня 2 | 11,42 | 14,30 | 2,55 | 36,47 | 3,49 | 32,98 | 0,04 | 13,60 | 4,40 |
| 9 | Коридор | 6,02 | 14,24 | 2,55 | 36,31 | 7,14 | 29,17 | 0,20 | 10,84 | нет |
| 10 | Спальня мастер | 22,48 | 20,02 | 2,55 | 51,05 | 7,48 | 43,57 | 0,09 | 18,52 | 8,99 |
| 11 | Ванная мастер | 2,13 | 5,84 | 2,56 | 14,98 | 1,47 | 13,51 | 0,04 | нет | нет |
| | **Итого** | **100,72** | | | **342,06** | **50,99** | **291,07** | **1,14** | **103,48** | **30,82** |

## Реестр контрольных сумм

| Показатель | По BOP | По чертежу | Расхождение | Лист |
|---|---|---|---|---|
| Σ площадей помещений без летних, м² — общая площадь по экспликации | 100,72 | 100,72 | 0,0 % | л. 14 |
| Стены под окраску, м² (шпаклёвка) ведомость отделки | 258,26 | 258,26 | 0,0 % | л. 54–56 |
| Потолки под окраску, м² — ведомость отделки | 100,72 | 100,72 | 0,0 % | л. 54–56 |
| Плинтус, м — ведомость отделки | 103,48 | 103,48 | 0,0 % | л. 54–56 |
| Плитка к заказу, шт — ведомость плитки | 124 | 124 | 0,0 % | л. 49 |
| Гидроизоляция, м² — ведомость материалов плитки | 17,01 | 17,01 | 0,0 % | л. 49 |
| Точки ЭОМ, шт — планы ЭОМ (без щитов) | 136 | 138 | -1,4 % | л. 23, 24 |

## Примечания

1. Объёмы — от геометрии проекта (та же, что на планах и в ведомости отделки), не от общей площади: P — периметр чистого контура, H — от чистого пола до низа потолка, проёмы — по наружному обводу коробок.
2. Подсчёт по ГЭСН-2001-15 и ГЭСН-2001-11: штукатурка и шпаклёвка стен — за вычетом проёмов; окраска водными составами — без вычета проёмов (п. 2.24); откосы — отдельно, по ширине до 200 и более 200 мм; полы — с площадью в дверных проёмах.
3. Плитка — по раскладке (целые и с подрезкой); короб инсталляции и фартук — отдельными строками, двойного счёта облицовки нет. Материалы, запас и количество к заказу — в спецификации материалов.
4. Цены — ориентир по открытым прайсам Москвы (цены на 21.09.2026), не коммерческое предложение; «по КП» — расценки нет, строка в итог не входит.
5. Демонтаж — по плану демонтажа и общим указаниям: покрытия пола, отделка стен и потолков, дверные блоки — до основания; объёмы справочные — по плану демонтажа (расценки в книге нет — «по КП»).
6. Штробы в стенах — только после технического заключения о несущих стенах (общие указания, план обмера и демонтажа): строка «Штробы в стенах» вертикальные спуски кабеля от потолочной трассы к точкам, объём не меньше фактического (горизонтальные трассы — по исполнительной схеме). Расценки штробления в прайсе нет — «по КП», в итог не входит; кабель в штробах стен прокладывается после неё.
7. Площадь облицовки стен — одно число с тремя названиями: зона облицовки по ведомости отделки 30,57 м² − место за коробом инсталляции 1,68 м² (плитку туда не кладут) = стены под плитку 28,89 м² (строка «Облицовка стен»); облицовка коробов 3,23 м² — отдельной строкой; стены и короба вместе — 32,12 м² (столько плитки по раскладке в спецификации). Источник — один (quantities.js), расхождение на листах ловит.
8. Слаботочные сети: кабель по лучам от ЩС** 90,70 м (U/UTP, RG-6, домофон — по видам), гофра 81,60 м, щит ЩС** с патч-панелью; розетки RJ45 и ТВ монтируются в строке «Электроточка». Длины те же, что в ведомости изделий электрика (одна модель — lowcurrent-engineer/bom.js); оборудование заказчика (точки доступа, камеры, коммутатор) в спецификацию не входит. 2 точ. — предложение листа слаботочки.
9. Коробы: стояков (нет) и К1 над чистым полом (7,07 м открытых участков; труба К1 вдоль стен 12,85 м в короб не зашивается — она за приборами, в раме инсталляции и в шахтах). В спецификации ВК короб К1 заказывается с запасом 10 % — 7,80 м. Материалы коробов стояков и инсталляции — в спецификации материалов, К1 — в спецификации ВК.

**Допущения и предложения на листе**

Основа листа: размеры сняты со скана обмерного плана KV оформление (см): часть подписей не читается, помещения выровнены по читаемым размерам; контрольный обмер не выполнен (К-1); высота потолка 2650 мм принята по отметкам обмера (H = 2,50…2,66 м, ригель 2,28 м) — уточнить при обмере (К-2); толщины стен 300 / 120 мм приняты, межквартирная стена и колонны — по скану, не замерены (К-1); разрешённая мощность 15 кВт принята по типовым ТУ; при объединении двух квартир — переоформление ТУ (К-4); подрайон климата не задан — принят не северный (жилые от 2,5 м) (К-8).

Знак «**» — предложение проектировщика, заказчиком не утверждено (согласовать с заказчиком): ЩС — щит слаботочный: место и состав.

См. лист открытых вопросов (лист 6, записи К-1, К-2, К-4, К-8).

| Изм. | Кол.уч | Лист | № док. | Подп. | Дата | | | | |
|---|---|---|---|---|---|---|---|---|---|
| Разраб. | | Кырлан А.С. | | | 04.11.26 | ГД-2026-009-АИ | | | |
| Пров. | | | | | | Квартира 103 м² | | | |
| ГИП | | | | | | Общая площадь 100,72* м² · * размеры со скана, не замерены (реестр — л. 6, 7, К-1) | | | |
| | | | | | | Дизайн-проект интерьера | Стадия | Лист | Листов |
| Н. контр. | | | | | | | РП | 116 | 120 |
| Утв. | | | | | | Ведомость объёмов работ (окончание) М б/м | Кырлан Александр Сергеевич | | |

выпуск 04.11.2026 № 35b47f1c2a · стр. 126 из 130

# Спецификация материалов

Отделочные материалы: чистое количество, запас, упаковка, к заказу · ГОСТ 21.110-2013

**ПРЕДВАРИТЕЛЬНО · не для производства работ · открыто пунктов: 8 (реестр — л. 6, 7)**

## Спецификация материалов (ГОСТ 21.110-2013, форма 1)

| Поз. | Наименование и техническая характеристика | Тип, марка, артикул | Код продукции | Поставщик | Ед. изм. | Количество | | | | Масса ед., кг | Примечание |
|---|---|---|---|---|---|---|---|---|---|---|---|
| | | | | | | чистое | запас, % | упаковка | к заказу | | |
| **Покрытия полов и облицовка** | | | | | | | | | | | |
| 1 | Инженерная доска (дуб натуральный, рабочий слой 4 мм, эмиссия E1, прямая укладка) | 1167-4250 | | | м² | 82,52 | 7 | по артикулу | 88,30 м² | | пом. 1, 2, 3, 5, 7, 8, 9, 10; до целой упаковки; л. 53–56 |
| 2 | Клей для паркетной и инженерной доски (эластичный, по ТУ изготовителя доски) | по выбору подрядчика | | | м² | 82,52 | | ведро по ТУ | по ТУ | | расход кг/м² — по ТУ клея; л. 53 |
| 3 | Керамогранит 600×600 мм Atlas Concorde Marvel Travertine Sand Cross 60×60 Matte Sensitech, арт. AFUL (той же коллекции, что стены A8UZ; тон сверить по образцу) | Atlas Concorde Marvel Travertine Sand Cross 60×60 Matte Sensitech, арт. AFUL (той же коллекции, что стены A8UZ; тон сверить по образцу) | | | шт | 23 | 10 | коробка | 26 шт | | 3 целых + 20 с подрезкой; 6,04 м² по раскладке, к заказу 9,36 м²; пом. 6, 11; л. 49–52 |
| 4 | Керамогранит 600×1200 мм A8UZ | A8UZ | | | шт | 86 | 10 | коробка | 98 шт | | 19 целых + 67 с подрезкой; 45,03 м² по раскладке, к заказу 70,56 м²; пом. 4, 6, 11; л. 49–52 |
| **Сухие смеси и гидроизоляция** | | | | | | | | | | | |
| 5 | Клей плиточный цементный класса C2 TE S1 (ГОСТ Р 56387-2018) | Ceresit CM 17 или аналог | | | кг | 364,55 | 10 | мешок 25 кг | 17 меш. | 25 | слой 5 мм, 1,50 кг/м² на 1 мм; л. 49 |
| 6 | Затирка цементная класса CG2WA, цвет — по колерной карте | Mapei Ultracolor Plus 132 или аналог | | | кг | 3,61 | 10 | упак. 2 кг | 2 упак. | 2 | расход (a+b)/ab × шов × t × 1,6 кг/м²; л. 49 |
| 7 | Гидроизоляция обмазочная полимерная, 2 слоя, лента в углах, манжеты на выводах | по выбору подрядчика | | | м² | 17,01 | 10 | ведро по ТУ | по ТУ | | пом. 6, 11; расход кг/м² — по ТУ; л. 49 |
| 8 | Лента демпферная по периметру пола из плитки | по выбору подрядчика | | | м | 24,68 | 10 | рулон | 28,00 м | | л. 49 |
| 9 | Смесь цементно-песчаная для стяжки М200 (50 мм, 49 мм, 47 мм, 33 мм) | по выбору подрядчика | | | м³ | 4,95 | 5 | мешок по ТУ | по ТУ | | S 101,85 м² × толщина; армирование и маяки — по ТУ; л. 53 |
| 10 | Смесь штукатурная гипсовая для машинного и ручного нанесения по маякам, слой до 10 мм | по выбору подрядчика | | | м² | 291,08 | 10 | мешок по ТУ | по ТУ | | пом. 1, 2, 3, 4, 5, 6, 7, 8, 9, 10, 11; расход кг/м² на 1 мм слоя — по ТУ смеси, толщина — по замеру кривизны стен; л. 14, 54–56 |
| **Короба из ГКЛВ** | | | | | | | | | | | |
| 11 | Лист ГКЛВ 12,5 мм, 2500 × 1200 мм, обшивка коробов в 2 слоя | по выбору подрядчика | | | м² | 6,46 | 10 | лист 3,00 м² | 3,00 лист | | инсталляция пом. 6: 1,76 м²; инсталляция пом. 11: 1,47 м²; площадь × 2 слоя; короб К1 над полом — в спецификации ВК; л. 33, 49–52 |
| 12 | Профиль стальной оцинкованный 27 × 28 мм: каркас коробов (стойки и направляющие) | по выбору подрядчика | | | м | 15,60 | 10 | хлыст 3 м | 6 шт | | стойки через 400 мм по свободному периметру + направляющие по полу и потолку; крепёж, лента, шпаклёвка швов — по узлу короба; л. 33, 49–52 |
| **Слаботочные сети** | | | | | | | | | | | |
| 13 | Кабель домофона — тип по системе поставщика | по выбору подрядчика | | | м | 4,30 | | бухта по ТУ | 5,00 м | | по лучам от ЩС**, 1 точ., запас 10 % уже в длине; 2 точ. — предложение листа слаботочки (знак «*» на плане); л. 30 |
| 14 | Кабель коаксиальный RG-6 (75 Ом) к розеткам ТВ | по выбору подрядчика | | | м | 16,10 | | бухта по ТУ | 17,00 м | | по лучам от ЩС**, 1 точ., запас 10 % уже в длине; 2 точ. — предложение листа слаботочки (знак «*» на плане); л. 30 |
| 15 | Кабель U/UTP кат. 6 (LAN, Wi-Fi и камеры по PoE) | по выбору подрядчика | | | м | 70,30 | | бухта по ТУ | 71,00 м | | по лучам от ЩС**, 5 точ., запас 10 % уже в длине; 2 точ. — предложение листа слаботочки (знак «*» на плане); л. 30 |
| 16 | Гофротруба Ø20 для слаботочных линий, отдельно от силовых | по выбору подрядчика | | | м | 81,60 | | бухта по ТУ | 82,00 м | | по длине лучей без участков в канале плинтуса (≈ 90 %); л. 30 |
| 17 | Розетка компьютерная RJ45, кат. 6, с рамкой и подрозетником | по выбору подрядчика | | | шт | 4 | | шт | 4 шт | | LAN1, LAN3, LAN4, LAN5**; серия механизмов — как у розеток и выключателей; л. 26, 27, 30 |

**Допущения и предложения на листе**

Основа листа: размеры сняты со скана обмерного плана KV оформление (см): часть подписей не читается, помещения выровнены по читаемым размерам; контрольный обмер не выполнен (К-1); высота потолка 2650 мм принята по отметкам обмера (Н = 2,50…2,66 м, ригель 2,28 м) — уточнить при обмере (К-2); толщины стен 300 / 120 мм приняты, межквартирная стена и колонны — по скану, не замерены (К-1); разрешённая мощность 15 кВт принята по типовым ТУ; при объединении двух квартир — переоформление ТУ (К-4); подрайон климата не задан — принят не северный (жилые от 2,5 м) (К-8).

Знак «**» — предложение проектировщика, заказчиком не утверждено (согласовать с заказчиком): LAN5 — стол Б2 стоит посреди помещения — питание из лючка в полу под столом: трасса в конструкции пола (толщина стяжки — по обмеру) — согласовать с заказчиком; ЩС — щит слаботочный: место и состав; плинтус пом. 1–5, 7–10, акцент пом. 3, фартук пом. 5 — артикул изделия не выбран: позиция описана характеристиками («аналог по характеристикам»), артикул выбирается при закупке; пол пом. 6, 11 — пирог пола: стяжка 33 мм и обмазочная гидроизоляция добавлены разработчиком проекта; артикул изделия не выбран: позиция описана характеристиками («аналог по характеристикам»), артикул выбирается при закупке.

См. лист открытых вопросов (лист 6, записи К-1, К-2, К-4, К-8).

| Изм. | Кол.уч | Лист | № док. | Подп. | Дата |
|---|---|---|---|---|---|
| Разраб. | | Кырлан А.С. | | | 04.11.26 |
| Пров. | | | | | |
| ГИП | | | | | |
| | | | | | |
| Н. контр. | | | | | |
| Утв. | | | | | |

**ГД-2026-009-АИ**

Квартира 103 м²

Общая площадь 100,72* м² · * размеры со скана, не замерены (реестр — л. 6, 7, К-1)

Дизайн-проект интерьера

| Стадия | Лист | Листов |
|---|---|---|
| РП | 117 | 120 |

**Спецификация материалов**

М б/м

**Кырлан Александр Сергеевич**

# Спецификация материалов (окончание)

Отделочные материалы: чистое количество, запас, упаковка, к заказу · ГОСТ 21.110-2013

## Спецификация материалов (ГОСТ 21.110-2013, форма 1) (продолжение)

| Поз. | Наименование и техническая характеристика | Тип, марка, артикул | Код продукции | Поставщик | Ед. изм. | Количество | | | | Масса ед., кг | Примечание |
|---|---|---|---|---|---|---|---|---|---|---|---|
| | | | | | | чистое | запас, % | упаковка | к заказу | | |
| 18 | Розетка телевизионная (коаксиальная) с рамкой и подрозетником | по выбору подрядчика | | | шт | 1 | | шт | 1 шт | | ТВ1; серия механизмов — как у розеток и выключателей; л. 26, 27, 30 |
| 19 | Трубка или монитор домофона (поставка домофонной организации) | по выбору подрядчика | | | шт | 1 | | шт | 1 шт | | ДФ1; серия механизмов — как у розеток и выключателей; л. 26, 27, 30 |
| 20 | Щит слаботочный ЩС**: корпус, DIN-рейка, розетки 220 В | по выбору подрядчика | | | шт | 1 | | шт | 1 шт | | ЩС**; серия механизмов — как у розеток и выключателей; л. 26, 27, 30 |
| 21 | Патч-панель, портов не менее 5 | по выбору подрядчика | | | шт | 1 | | шт | 1 шт | | серия механизмов — как у розеток и выключателей; л. 26, 27, 30 |
| **Лакокрасочные материалы** | | | | | | | | | | | |
| 22 | Краска интерьерная акриловая, матовая, класс истирания 1 | Farrow & Ball Modern Emulsion No. 289 «Inchyra Blue — тёмный сине-серый» | | | л | 8,54 | 10 | банка 2,5 л | 4 банк | | 35,60 м² × 2 сл. × 0,12 л/м²; пом. 1, 8, 10; л. 54–56 |
| 23 | Краска интерьерная акриловая, матовая, класс истирания 1 | Farrow & Ball Modern Emulsion No. 291 «School House White — тёплый меловой белый» | | | л | 49,98 | 10 | банка 2,5 л | 22 банк | | 208,26 м² × 2 сл. × 0,12 л/м²; пом. 1, 3, 3 (пот.), 4, 5, 5 (пот.), 8, 9, 10; л. 54–56 |
| 24 | Краска интерьерная акриловая, глубокоматовая, класс истирания 2 | Tikkurila Anti-Reflex 2 S 0502-Y «Белый с лёгкой желтизной» | | | л | 16,28 | 10 | банка 2,7 л | 7 банк | | 67,84 м² × 2 сл. × 0,12 л/м²; пом. 1 (пот.), 2 (пот.), 4 (пот.), 7 (пот.), 8 (пот.), 9 (пот.), 10 (пот.); л. 54–56 |
| 25 | Краска интерьерная акриловая, матовая, класс истирания 1 | Tikkurila Harmony S 0502-Y «Белый с лёгкой желтизной» | | | л | 7,08 | 10 | банка 2,7 л | 3 банк | | 29,50 м² × 2 сл. × 0,12 л/м²; пом. 2, 7; л. 54–56 |
| 26 | Краска интерьерная акриловая, матовая, класс истирания 1 | Farrow & Ball Modern Emulsion No. 255 «Tanner's Brown — тёмный шоколад» | | | л | 4,23 | 10 | банка 2,5 л | 2 банк | | 11,74 м² × 3 сл. × 0,12 л/м²; пом. 3; л. 54–56 |
| 27 | Краска интерьерная акриловая, матовая, класс истирания 1 | Tikkurila Luja 7 S 0502-Y «Белый с лёгкой желтизной» | | | л | 1,45 | 10 | банка 2,7 л | 1 банк | | 6,04 м² × 2 сл. × 0,12 л/м²; пом. 6 (пот.), 11 (пот.); л. 54–56 |
| 28 | Шпаклёвка финишная полимерная под окраску (стены и потолки, Q3) | по выбору подрядчика | | | м² | 358,98 | 10 | ведро по ТУ | по ТУ | | расход кг/м² на слой — по ТУ; л. 54–56 |
| 29 | Грунтовка акриловая глубокого проникновения, 2 слоя | по выбору подрядчика | | | м² | 391,80 | 10 | канистра по ТУ | по ТУ | | расход л/м² — по ТУ; л. 54–56 |
| **Погонажные изделия и потолки** | | | | | | | | | | | |
| 30 | Плинтус напольный МДФ под покраску, h=83 мм, крепление к стене | Ultrawood Base 5340, ЛДФ под окраску, 83×15 мм, 2440 мм (арт. LDF-BASE-5340) | | | м.п. | 103,48 | 10 | хлыст 2,4 м | 48 шт | | пом. 1, 2, 3, 4, 5, 7, 8, 9, 10; длина хлыста — по артикулу; л. 54–56 |
| 31 | Потолок подвесной ГКЛ/ГКЛВ по каркасу Knauf П113: листы, профили, подвесы, лента, шпаклёвка швов | Knauf П113 | | | м² | 96,28 | | комплект | по л. потолков | | площадь — по ведомости потолков; число листов, профилей и подвесов — по шагам каркаса на листе потолков; л. 45–48 |

## Примечания

1. Чистое количество — из ведомости объёмов работ и раскладки плитки; запас — отдельной графой (доска — по ведомости отделки, плитка, краска и плинтус — 10 %); «к заказу» — с запасом и кратно упаковке.
2. Плитка — штуками по раскладке, запас на каждую поверхность. Калибр (рабочий размер) и тон — одной партией на помещение, калибр указать при заказе и сверить с раскладкой до укладки.
3. Краска — 0,12 л/м² на слой (середина вилки 0,10–0,15 л/м²) по фактической площади окраски из ведомости отделки; колеровка одной партией.
4. «По ТУ» — расход задаёт производитель выбранного продукта; количество к заказу — после выбора марки.
5. Штукатурная смесь — на ту же площадь, что строка ВОР «Штукатурка стен» (291,08 м²): площадь одна, расход смеси задаёт производитель.
6. Коробы инсталляции и стояков: ГКЛВ в 2 слоя и профиль 27 × 28 мм считаются по свободным граням коробов (источник — раскладка плиточника и шахты в данных); короб К1 над полом — в спецификации ВК.
7. Потолки ГКЛ: в этой спецификации — площадь системы П113; число листов, профилей и подвесов — по шагам каркаса на листе потолков (подвесы через 1000, несущие через 500, основные через 1200 мм), схема каркаса не выпущена. Сантехника, светильники и мебель — по своим спецификациям.

**Допущения и предложения на листе**

Основа листа: размеры сняты со скана обмерного плана KV оформление (см): часть подписей не читается, помещения выровнены по читаемым размерам; контрольный обмер не выполнен (К-1); высота потолка 2650 мм принята по отметкам обмера (Н = 2,50…2,66 м, ригель 2,28 м) — уточнить при обмере (К-2); толщины стен 300 / 120 мм приняты, межквартирная стена и колонны — по скану, не замерены (К-1); разрешённая мощность 15 кВт принята по типовым ТУ; при объединении двух квартир — переоформление ТУ (К-4); подрайон климата не задан — принят не северный (жилые от 2,5 м) (К-8).

Знак «**» — предложение проектировщика, заказчиком не утверждено (согласовать с заказчиком): ЩС — щит слаботочный: место и состав; плинтус пом. 1–5, 7–10, акцент пом. 3, фартук пом. 5 — артикул изделия не выбран: позиция описана характеристиками («аналог по характеристикам»), артикул выбирается при закупке; пол пом. 6, 11 — пирог пола: стяжка 33 мм и обмазочная гидроизоляция добавлены разработчиком проекта; артикул изделия не выбран: позиция описана характеристиками («аналог по характеристикам»), артикул выбирается при закупке.

См. лист открытых вопросов (лист 6, записи К-1, К-2, К-4, К-8).

| Изм. | Кол.уч | Лист | № док. | Подп. | Дата | | | |
|---|---|---|---|---|---|---|---|---|
| Разраб. | | Кырлан А.С. | | | 04.11.26 | ГД-2026-009-АИ | | |
| Пров. | | | | | | Квартира 103 м² | | |
| ГИП | | | | | | Общая площадь 100,72* м² · * размеры со скана, не замерены (реестр — л. 6, 7, К-1) | | |
| | | | | | | Дизайн-проект интерьера | Стадия: РП; Лист: 118; Листов: 120 | |
| Н. контр. | | | | | | Спецификация материалов (окончание) М б/м | Кырлан Александр Сергеевич | |
| Утв. | | | | | | | | |

# Смета ориентировочная

**ПРЕДВАРИТЕЛЬНО · не для производства работ · открыто пунктов: 8 (реестр — л. 6, 7)**

Работы, материалы, оборудование, услуги и резерв · цены — ориентир по открытым прайсам, не коммерческое предложение

## Сводная смета (цены на 21.09.2026, Москва)

| № | Наименование работ, материалов, услуг | Ед. изм. | Кол-во | Цена за ед., ₽ | Стоимость, ₽ | | | Чей подряд | Срок поставки, дн. | Основание | Источник цены |
|---|---|---|---|---|---|---|---|---|---|---|---|
| | | | | | план | факт | разница | | | | |
| **Работы — по ведомости объёмов работ** | | | | | | | | | | | |
| 1 | Демонтаж и черновые работы (без 5 поз. по КП) | раздел | 1 | | 364 151 | | | бригада | | ВОР, поз. 1–10; л. 114–116 | по ВОР |
| 2 | Инженерные системы (без 12 поз. по КП) | раздел | 1 | | 190 135 | | | бригада | | ВОР, поз. 11–33; л. 114–116 | по ВОР |
| 3 | Чистовые работы (без 1 поз. по КП) | раздел | 1 | | 809 479 | | | бригада, поставщик | | ВОР, поз. 34–50; л. 114–116 | по ВОР |
| **Материалы — по спецификации материалов** | | | | | | | | | | | |
| 4 | Инженерная доска | м² | 88,30 | 4 513 | 398 498 | | | поставщик | | спецификация, поз. 1 | Ц7 |
| 5 | Керамогранит 600×600 мм | м² | 9,36 | 1 800 | 16 848 | | | поставщик | | спецификация, поз. 3 | Ц6 |
| 6 | Керамогранит 600×1200 мм | м² | 70,56 | 3 500 | 246 960 | | | поставщик | | спецификация, поз. 4 | Ц6 |
| 7 | Клей плиточный цементный класса C2 TE S1 | меш. | 17 | 1 800 | 30 600 | | | поставщик | | спецификация, поз. 5 | Ц7 |
| 8 | Затирка цементная класса CG2WA | упак. | 2 | 1 000 | 2 000 | | | поставщик | | спецификация, поз. 6 | Ц7 |
| 9 | Краска Farrow & Ball Modern Emulsion, банка 2,5 л | банк | 28 | 5 800 | 162 400 | | | поставщик | | спецификация, поз. 22, 23, 26 | Ц7 |
| 10 | Краска Tikkurila (Anti-Reflex 2, Harmony, Luja 7), банка 2,7 л | банк | 11 | 3 510 | 38 610 | | | поставщик | | спецификация, поз. 24, 25, 27 | Ц6 |
| 11 | Плинтус напольный МДФ под покраску | шт | 48 | 368 | 17 664 | | | поставщик | | спецификация, поз. 30 | Ц7 |
| 12 | Прочие материалы с расходом по ТУ (клей для доски, гидроизоляция, демпферная лента, смесь для стяжки, смесь штукатурная гипсовая для машинного и ручного нанесения по маякам, лист гклв 12, профиль стальной оцинкованный 27 × 28 мм: каркас коробов (стойки и направляющие), кабель слаботочки, гофра слаботочки, изделия слаботочки, шпаклёвка, грунтовка, каркас и ГКЛ потолков) | компл | 1 | по КП | | | | поставщик | | спецификация, поз. 2, 7, 8, 9, 10, 11, 12, 13, 14, 15, 16, 17, 18, 19, 20, 21, 28, 29, 31 | |
| **Оборудование и мебель — поставка по спецификациям** | | | | | | | | | | | |
| 13 | Кухонный гарнитур по проекту кухни, изготовление и монтаж (4–8 нед.) | компл | 1 | по КП | | | | поставщик | не задан; ориентир 4–8 нед. от замера | л. 72–75 | |

**Допущения и предложения на листе**

Основа листа: размеры сняты со скана обмерного плана KV оформление (см): часть подписей не читается, помещения выровнены по читаемым размерам; контрольный обмер не выполнен (К-1); высота потолка 2650 мм принята по отметкам обмера (Н = 2,50…2,66 м, ригель 2,28 м) — уточнить при обмере (К-2); толщины стен 300 / 120 мм приняты, межквартирная стена и колонны — по скану, не замерены (К-1); разрешённая мощность 15 кВт принята по типовым ТУ; при объединении двух квартир — переоформление ТУ (К-4); подрайон климата не задан — принят не северный (жилые от 2,5 м) (К-8).

См. лист открытых вопросов (лист 6, записи К-1, К-2, К-4, К-8).

| Изм. | Кол.уч | Лист | № док. | Подп. | Дата |
|---|---|---|---|---|---|
| Разраб. | | Кырлан А.С. | | | 04.11.26 |
| Пров. | | | | | |
| ГИП | | | | | |
| | | | | | |
| Н. контр. | | | | | |
| Утв. | | | | | |

**ГД-2026-009-АИ**

Квартира 103 м²

Общая площадь 100,72* м² · * размеры со скана, не замерены (реестр — л. 6, 7, К-1)

Дизайн-проект интерьера

| Стадия | Лист | Листов |
|---|---|---|
| РП | 119 | 120 |

**Смета ориентировочная**

М б/м

**Кырлан Александр Сергеевич**

# Смета ориентировочная (окончание)

Работы, материалы, оборудование, услуги и резерв · цены — ориентир по открытым прайсам, не коммерческое предложение

## Сводная смета (цены на 21.09.2026, Москва) (продолжение)

| № | Наименование работ, материалов, услуг | Ед. изм. | Кол-во | Цена за ед., ₽ | Стоимость, ₽ | | | Чей подряд | Срок поставки, дн. | Основание | Источник цены |
|---|---|---|---|---|---|---|---|---|---|---|---|
| | | | | | план | факт | разница | | | | |
| 14 | Двери скрытого монтажа с коробом под покраску, поставка | шт | 8 | по КП | | | | поставщик | не задан; ориентир ≈ 30 дн. | л. 16, 17 | |
| 15 | Оборудование заказчика слаботочных сетей: точка доступа wi-fi — 1 шт; коммутатор — 1 шт | компл | 1 | по КП | | | | заказчик | | л. 26, 27 | |
| 16 | Сантехника, светильники, мебель и предметы интерьера | компл | 1 | по КП | | | | поставщик | | л. 42; л. 43, 44; л. 77; л. 20–22 | |
| **Прочие работы и услуги** | | | | | | | | | | | |
| 17 | Вынос и вывоз строительного мусора | м³ | | по факту | | | | бригада | | после демонтажа | |
| 18 | Подъём материалов на этаж (лифтом или вручную — по договору) | т | | по факту | | | | бригада | | по массе поставки | |
| 19 | Доставка чистовых материалов, 10 % от поставки | | | 10 % | 91 358 | | | поставщик | | от суммы материалов | |
| 20 | Уборка после ремонта | м² | 100,72 | по факту | | | | бригада | | S квартиры | |
| | **Итого работы** | | | | **1 363 765** | | | | | | |
| | **Итого материалы** | | | | **913 580** | | | | | | |
| | **Итого прочие услуги** | | | | **91 358** | | | | | | |
| | **Резерв на непредвиденные работы и материалы, 15 %** | | | | **355 305** | | | | | | |
| | **ВСЕГО ориентировочно (без оборудования и позиций по КП)** | | | | **2 724 008** | | | | | | |

## Примечания

1. Смета ориентировочная, не коммерческое предложение: объёмы — из ведомости объёмов работ и спецификации материалов, цены — нижняя граница открытых прайсов Москвы (цены на 21.09.2026); перед договором цены подтвердить у подрядчика и поставщиков.
2. Источники цен: Ц1 — Домашний мастерок: прайс на отделочные работы, 2026; Ц2 — Домашний мастерок: прайс на плиточные работы, 2026; Ц3 Домашний мастерок: прайс на электромонтажные работы, 2026; Ц4 — Профи ремонтник: штукатурно-малярные работы; Ц5 — Profi.ru: укладка керамогранита на стены, Москва 2026; Ц6 — knowledge/spec-materials.md, разд. 1 и 3: ориентир по сегментам; Ц7 — Розница Москвы, 09.2026: Лемана ПРО, KGSnab, официальный дилер Farrow & Ball.
3. В итог не вошли позиции «по КП» и «по факту»: оборудование и мебель, двери, материалы с расходом по ТУ, вывоз мусора, подъём и уборка.
4. Доставка — 10 % от материалов, резерв — 15 % (частный ремонт 10–20 %) отдельными строками, в количествах не спрятаны. Графы «факт» и «разница» заполняются по актам.

**Допущения и предложения на листе**

Основа листа: размеры сняты со скана обмерного плана KV оформление (см): часть подписей не читается, помещения выровнены по читаемым размерам; контрольный обмер не выполнен (К-1); высота потолка 2650 мм принята по отметкам обмера (Н = 2,50…2,66 м, ригель 2,28 м) — уточнить при обмере (К-2); толщины стен 300 / 120 мм приняты, межквартирная стена и колонны — по скану, не замерены (К-1); разрешённая мощность 15 кВт принята по типовым ТУ; при объединении двух квартир — переоформление ТУ (К-4); подрайон климата не задан — принят не северный (жилые от 2,5 м) (К-8).
См. лист открытых вопросов (лист 6, записи К-1, К-2, К-4, К-8).

| Изм. | Кол.уч | Лист | № док. | Подп. | Дата |
|---|---|---|---|---|---|
| Разраб. | | Кырлан А.С. | | | 04.11.26 |
| Пров. | | | | | |
| ГИП | | | | | |
| | | | | | |
| Н. контр. | | | | | |
| Утв. | | | | | |

**ГД-2026-009-АИ**

Квартира 103 м²

Общая площадь 100,72* м² · * размеры со скана, не замерены (реестр — л. 6, 7, К-1)

Дизайн-проект интерьера

| Стадия | Лист | Листов |
|---|---|---|
| РП | 120 | 120 |

**Смета ориентировочная (окончание)**

М б/м

**Кырлан Александр Сергеевич**