
LINEA

ДИЗАЙН-ПРОЕКТ ИНТЕРЬЕРА

Квартира 101 м²

ретро с авторской мебелью

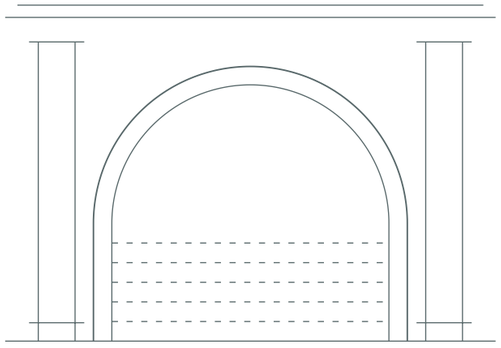


ПАЛИТРА ОТДЕЛКИ

F&B No. 291	NCS S 0502-Y	F&B No. 289	F&B No. 255	NCS S 1005-Y20
58 %	29 %	10 %	3 %	текстиль, декор

АВТОР ПРОЕКТА

Кырлан Александр Сергеевич

Ноябрь 2026

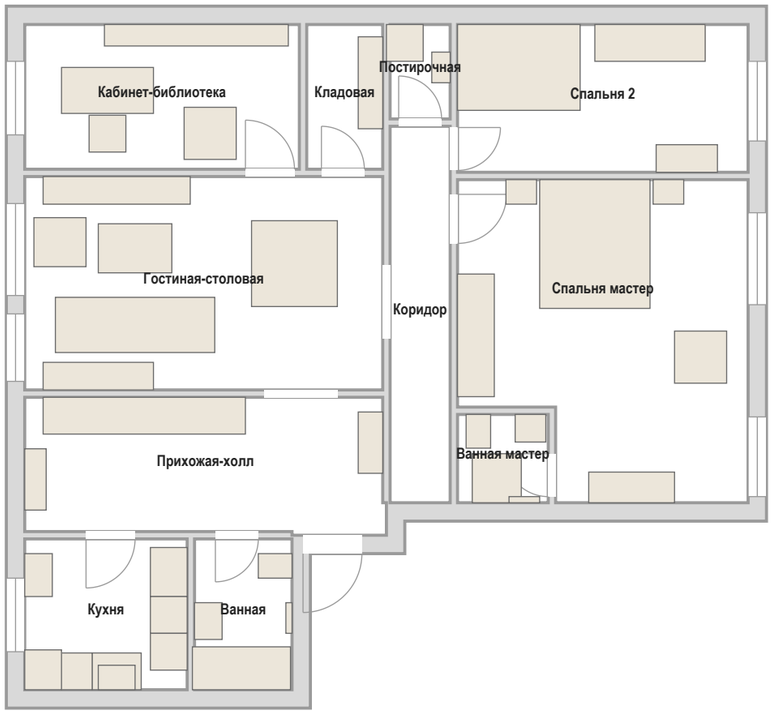

План расстановки мебели · М 1:100

ОБЩАЯ ПЛОЩАДЬ	ПОМЕЩЕНИЙ	СТАДИЯ	ШИФР	ОСНОВА
100,72 м²	11, из них жилых 4	Проект · предварительно	ГД-2026-009-АИ	план заказчика, без обмера

Как оставить правку: кнопка «Правка к этому листу» в правом верхнем углу любого листа · все листы проекта: дизайн-студия-квартир.рф/review.html?p=gost-retro103

выпуск 04.11.2026 № d6a6e5e88d · стр. 1 из 96

Объект

Квартира 103 м²: 100,72 м², помещений 11, из них жилых 4.

Стиль: мид-сенчури 65 %, ар-деко 35 %. Стадия: предварительный альбом без обмера, планировка по плану заказчика.

Открытых вопросов 7, конфликтов разделов 0; изменений утверждено 0, ждут подписи 1.

Розетки и выводы

38 розеток (рамок 33), 6 выводов кабеля под технику и свет, 14 групп щита — всё с высотами от чистого пола: листы 36, 37.

Что решено (подписано вами)

Подписанных решений пока нет.

Что ждёт вашего ответа

К-1 — Размеры сняты со скана обмерного плана KV оформление (в см): часть подписей не читается, помещения выровнены по читаемым размерам.

К-2 — Высота потолка принята 2650 мм по отметкам обмера (Н = 2,50…2,66 м).

К-4 — Разрешённая мощность объединённой квартиры по ТУ неизвестна, принята 15 кВт.

К-5 — Объединение двух квартир в одну (проём в межквартирной стене между гостиной и коридором правой квартиры, вход — один из тамбура, второй вход закрывается.

К-6 — Ванная мастер (пом. 11): стояки Ст К1-3 Ø110, Ст В1-3, Ст Т3-3 по данным стоят в углу стен В и Г (оси ≈ 90–240 мм от стены Г, 150–280 мм от стены В) — внутри габарита душевого…

К-7 — Унитаз подвесной С_02 (пом. 6 «Ванная»), выпуск К1-2 Ø110: трасса до Ст К1-1 (1,91 м) идёт под дверным проёмом Д-5 — короб над полом там не поставить.

К-8 — Климатический подрайон (СП 131.13330) не задан: принят не северный — жилые комнаты и кухня под потолком от 2,5 м (СП 54, п. 5.12).

Предложено, ждёт подписи

ИЗ-1 — Группы 7 (санузлы: фены, полотенцесушители, УЗО 10 мА) и 8 (стиральная машина постирочной) добавлены, точки переназначены.

выпуск 04.11.2026 № d6a6e6e88d · стр. 2 из 96

					Проект: Квартира 103 м²
	Лист	№ док.	Подпись	Дата	Ваш проект на одной странице
Дизайнер	Кырлан А.С.			04.11.26	

Стадия	Лист	Листов
П	2	96

Список листов

Лист	Наименование
1	Титульный лист
2	Ваш проект на одной странице
3	Список листов
4	Как читать альбом
5	План планировки от заказчика
6	План монтажный
7	Кухня (пом. 5). Монтажная схема
8	Кухня (пом. 5). Монтажная схема
9	Шкафы. Монтажная схема
10	Карта покрытий стен
11	Колерная карта
12	Колерная карта
13	План размещения мебели и оборудования
14	Спецификация мебели и оборудования
15	Спецификация мебели и оборудования (продолжение)
16	Спецификация мебели и оборудования (продолжение)
17	Ведомости изделий, техники и фурнитуры
18	План выводов сантехники
19	Схема разводки водопровода и канализации
20	Аксонометрическая схема В1 (холодное водоснабжение)
21	Аксонометрическая схема Т3 (горячее водоснабжение)
22	Аксонометрическая схема К1 (канализация)
23	Развёртки мокрых зон: выводы ВК. Кухня
24	Развёртки мокрых зон: выводы ВК. Ванная
25	Развёртки мокрых зон: выводы ВК. Постирочная
26	Развёртки мокрых зон: выводы ВК. Ванная мастер
27	Спецификация сантехнического оборудования
28	Раскладка плитки. Ванная. Развёртки стен
29	Раскладка плитки. Ванная мастер. Развёртки стен
30	План размещения дверей
31	Ведомость заполнения проёмов
32	План потолков
33	Разрезы и узлы потолков
34	Разрезы и узлы потолков (продолжение)
35	Сечения потолков М 1:10
36	Однолинейная схема щита
37	План розеток и электровыводов
38	План слаботочных сетей
39	План освещения
40	Техническое задание на подбор светильников
41	Управление светильниками
42	План вентиляции
43	План отопления
44	План покрытий пола
45	Раскладка плитки. Планы полов
46	Раскладка плитки. Прихожая-холл
47	Развёртка стены А. Кабинет-библиотека (пом. 1)
48	Развёртки стен Б, Г. Кабинет-библиотека (пом. 1)
49	Развёртка стены В. Кабинет-библиотека (пом. 1)
50	Развёртки стен. Кладовая (пом. 2)
51	Развёртка стены А. Гостиная-столовая (пом. 3)
52	Привязки электроточек, стена А. Гостиная-столовая (пом. 3)
53	Развёртка стены Б. Гостиная-столовая (пом. 3)
54	Развёртка стены В. Гостиная-столовая (пом. 3)
55	Развёртка стены Г. Гостиная-столовая (пом. 3)
56	Развёртка стены А. Прихожая-холл (пом. 4)
57	Развёртки стен Б, Г. Прихожая-холл (пом. 4)
58	Развёртка стены В. Прихожая-холл (пом. 4)
59	Развёртка стены Б. Кухня (пом. 5), кухонный фронт
60	Привязки электроточек и выводов ВК, стена Б. Кухня (пом. 5)
61	Развёртка стены В. Кухня (пом. 5), кухонный фронт
62	Развёртки стен А, Г. Кухня (пом. 5)
63	Развёртки стен А, Б. Ванная (пом. 6)
64	Развёртки стен В, Г. Ванная (пом. 6)
65	Привязки электроточек и выводов ВК, стена Г. Ванная (пом. 6)
66	Развёртки стен А, Б, В. Постирочная (пом. 7)
67	Развёртка стены Г. Постирочная (пом. 7)
68	Развёртка стены А. Спальня 2 (пом. 8)
69	Развёртки стен Б, Г. Спальня 2 (пом. 8)
70	Развёртка стены В. Спальня 2 (пом. 8)
71	Развёртка стены А. Коридор (пом. 9)
72	Развёртка стены Б. Коридор (пом. 9)
73	Развёртка стены В. Коридор (пом. 9)
74	Развёртка стены А. Спальня мастер (пом. 10)
75	Привязки электроточек, стена А. Спальня мастер (пом. 10)
76	Развёртка стены Б. Спальня мастер (пом. 10)
77	Развёртка стены В. Спальня мастер (пом. 10)
78	Развёртка стены Г1. Спальня мастер (пом. 10)
79	Развёртка стены Г2. Спальня мастер (пом. 10)
80	Развёртки стен А, Б, В. Ванная мастер (пом. 11)
81	Привязки электроточек и выводов ВК, стена А. Ванная мастер (пом. 11)
82	Развёртка стены Г. Ванная мастер (пом. 11)
83	Открытые вопросы, принятые допущения и конфликты
Д_1	Система хранения М_05
Д_2	Шкаф-купе М_11
Д_3	Система хранения М_22
Д_4	Шкаф распашной М_24
Д_5	Шкаф распашной М_29
Д_6	Кухня (пом. 5). Развёртка гарнитура
Д_7	Кухня (пом. 5). Развёртка гарнитура
С1	Ведомость отделки помещений. Лист 1 из 2
С2	Ведомость отделки помещений. Лист 2 из 2
С3	Спецификация отделочных материалов
С4	Список покупок
С5	Список покупок (окончание)
С6	Узлы

Общие указания

1. Размеры даны в мм от чистовых поверхностей стен: слой штукатурки 20 мм по блоку и 5 мм шпаклёвки по ГКЛ учтён. Перед заказом встроенной мебели — контрольный обмер после штукатурки.
2. Привязки мебели — от стен и углов помещения, а не от другой мебели.
3. Розетки, выводы и выключатели под мебель — см. лист 37 «План розеток и электровыводов»; сантехприборы и выводы воды — лист 18.
4. План расстановки не является документацией для изготовления мебели: изделия — по чертежам мебельщика; покупную мебель заменять только на изделия не больше габарита из спецификации (лист 14).
5. Встроенная мебель «стена в стену» — с зазором 10 мм с каждой стороны или с компенсаторами.
6. Развёртки — вид на стену изнутри помещения, по часовой стрелке; расположение стен на схеме листа развёртки; размеры — в мм по чистовым поверхностям; отметки — в м от ±0,000; высоты Н — от чистого пола помещения до оси изделия, у декора — до центра.
7. Красная цепочка — привязки электроточек и выводов по осям от угла чистовых стен; высота Н — у знака, от чистого пола до оси; высоты мебели, проёмов и границ отделки колонкой отметок слева. Стена с 5 и более точками или с мелкими звеньями привязок показана двумя видами: архитектурная развёртка (мебель, отделка, проёмы, высоты) и вид «Привязки» на отдельном листе — точки и выводы с марками, одна цепочка по осям и таблица привязок (каждая точка — строка).
8. У знака электроточки: марка (Р — розетка, S — выключатель, Св — светильник, ЭВ вывод кабеля), ×N — число постов в рамке, гр. — группа щита, Н — высота оси от чистого пола, мм; группы по клавишам выключателя — на листе выключателей.
9. Схема мебели, приборов и декора не является технической документацией для производства мебели; габариты — по паспортам изделий.
10. Марки позиций: М_NN — мебель, ОБ_NN — оборудование, С_NN — сантехника; О-N отделка (ведомость отделочных материалов, серия С).
11. Размеры мебели и изделий на заказ уточнить по месту после отделочных работ.

					Проект: Квартира 103 м²			
	Лист	№ док.	Подпись	Дата	Список листов	Стадия	Лист	Листов
Дизайнер	Кырлан А.С.			04.11.26		П	3	96

Что в альбоме

Альбом — дизайн-проект с рабочими чертежами для ремонта. Листы идут в порядке работ: титул и вводные, реестр открытых вопросов и решений, планы (обмер, монтаж стен, мебель, двери, потолки, полы), инженерия (сантехника, электрика, вентиляция и отопление), развёртки стен с визуализациями помещений, чертежи мебели, ведомости материалов и узлы.

Вам как заказчику — титул, эта вводная, «Ваш проект на одной странице», реестр вопросов, план мебели, визуализации и развёртки, ведомости мебели и материалов. Подрядчику — всё остальное: монтажные планы, привязки выводов и розеток, узлы, ведомости объёмов.

Знаки на листах

Без знака — решение утверждено или подтверждено обмером.

Что проверить до ремонта

1. Розетки у кровати и рабочего места: хватает ли их с каждой стороны кровати и над столом (план розеток — лист 37).

2. Выводы под технику — варочная панель, духовка, посудомойка, стиральная машина, бойлер: совпадают ли с выбранными моделями (листы 14, 15, 16, 37).

3. Высоты розеток, выключателей и выводов даны от чистого пола: если мебель или техника будут другими — скажите до штробления стен.

Номера записей

К-N — открытый вопрос: чего не хватает или что выбрать (варианты и рекомендация — в тексте). Пока ответа нет, действует строка «если решения нет».

Кф-N — конфликт между разделами (например, мебель и радиатор в одном месте); закрывается решением, которое записывается как ИЗ-N.

ИЗ-N — изменение проекта: что было, что стало и кто утвердил. Изменение без подписи предложение.

Все записи — на листе реестра сразу после вводных; на других листах на них стоят ссылки.

Почему альбом предварительный


Обмера на объекте не было: размеры взяты с плана заказчика. Технические условия (мощность, вода, вентиляция дома) не получены, часть решений ждёт вашего ответа. Пока в реестре есть открытые вопросы, альбом предварительный — пометка в штампе снимается закрытием вопросов, а не стиранием.

Правку к любому листу можно оставить по кнопке «Правка к листу» или на сайте студии: дизайн-студия-квартир.рф — укажите номер листа и что изменить.

3 круга правок входят в цену; условия — в договоре и на странице вашего заказа на сайте студии.

Отметки по высоте

±0,000	чистый пол пом. 1–5, 7–10; отсчёт высот
−0,015	чистый пол пом. 6, 11, ниже на 15 мм
−0,064	верх плиты — расчёт, не замер (задание на обмер)
сущ. пол	снимается до плиты; не замерен (задание на обмер)

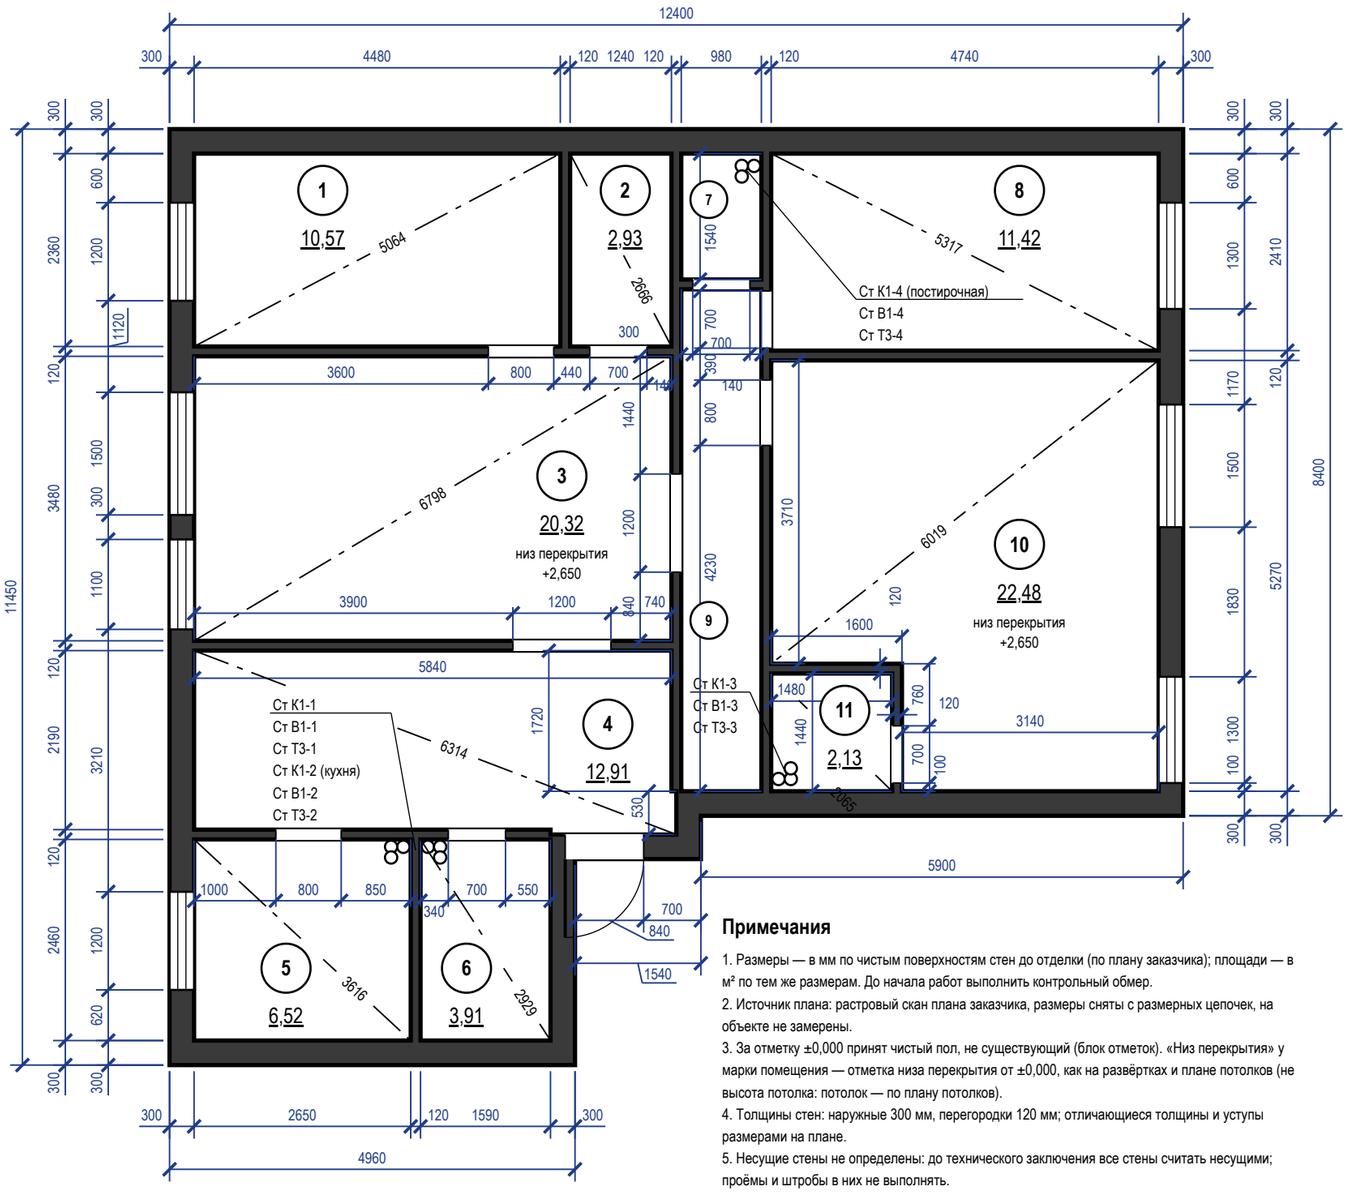

Экспликация помещений

№	Наименование	Площадь, м²
1	Кабинет-библиотека	10,57
2	Кладовая	2,93
3	Гостиная-столовая	20,32
4	Прихожая-холл	12,91
5	Кухня	6,52
6	Ванная	3,91
7	Постирочная	1,51
8	Спальня 2	11,42
9	Коридор	6,02
10	Спальня мастер	22,48
11	Ванная мастер	2,13
	Итого (общая площадь)	**100,72**


Условные обозначения

- существующие стены (сечение)
- окно (рама, остекление)
- проём существующий, без заполнения (откосы)
- стояк: К1 — канализация, В1 — ХВС, Т3 — ГВС
- диагональ помещения — контроль прямоугольности
- (1) номер помещения, площадь м²

Примечания

1. Размеры — в мм по чистым поверхностям стен до отделки (по плану заказчика); площади — в м² по тем же размерам. До начала работ выполнить контрольный обмер.
2. Источник плана: растровый скан плана заказчика, размеры сняты с размерных цепочек, на объекте не замерены.
3. За отметку ±0,000 принят чистый пол, не существующий (блок отметок). «Низ перекрытия» у марки помещения — отметка низа перекрытия от ±0,000, как на развёртках и плане потолков (не высота потолка: потолок — по плану потолков).
4. Толщины стен: наружные 300 мм, перегородки 120 мм; отличающиеся толщины и уступы размерами на плане.
5. Несущие стены не определены: до технического заключения все стены считать несущими; проёмы и штробы в них не выполнять.
6. Дверные проёмы показаны без заполнения (двери — лист 31); высота дверных проёмов 2100 мм, проёмов без двери 2100 мм; низ окон (подоконник) 720, 735, 763, 783, 825 мм от чистого пола, высота окон 1560, 1550, 1552, 1548 мм.
7. Диагонали — контрольные размеры; расхождение более 5 мм подписать на плане как перекос.
8. Размеры проверить на месте до начала работ; расхождение контрольных промеров ≤ 2 %.
9. Размеры короче 1 мм на листе цепочкой не показаны (две выносные линии на таком расстоянии сливаются): пом. 9, стена Б — 20 мм от угла до проёма.

					Проект: Квартира 103 м²	**М 1:75**
	Лист	№ док.	Подпись	Дата	План планировки от заказчика	Стадия / Лист / Листов
Дизайнер	Кырлан А.С.			04.11.26		П / 5 / 96

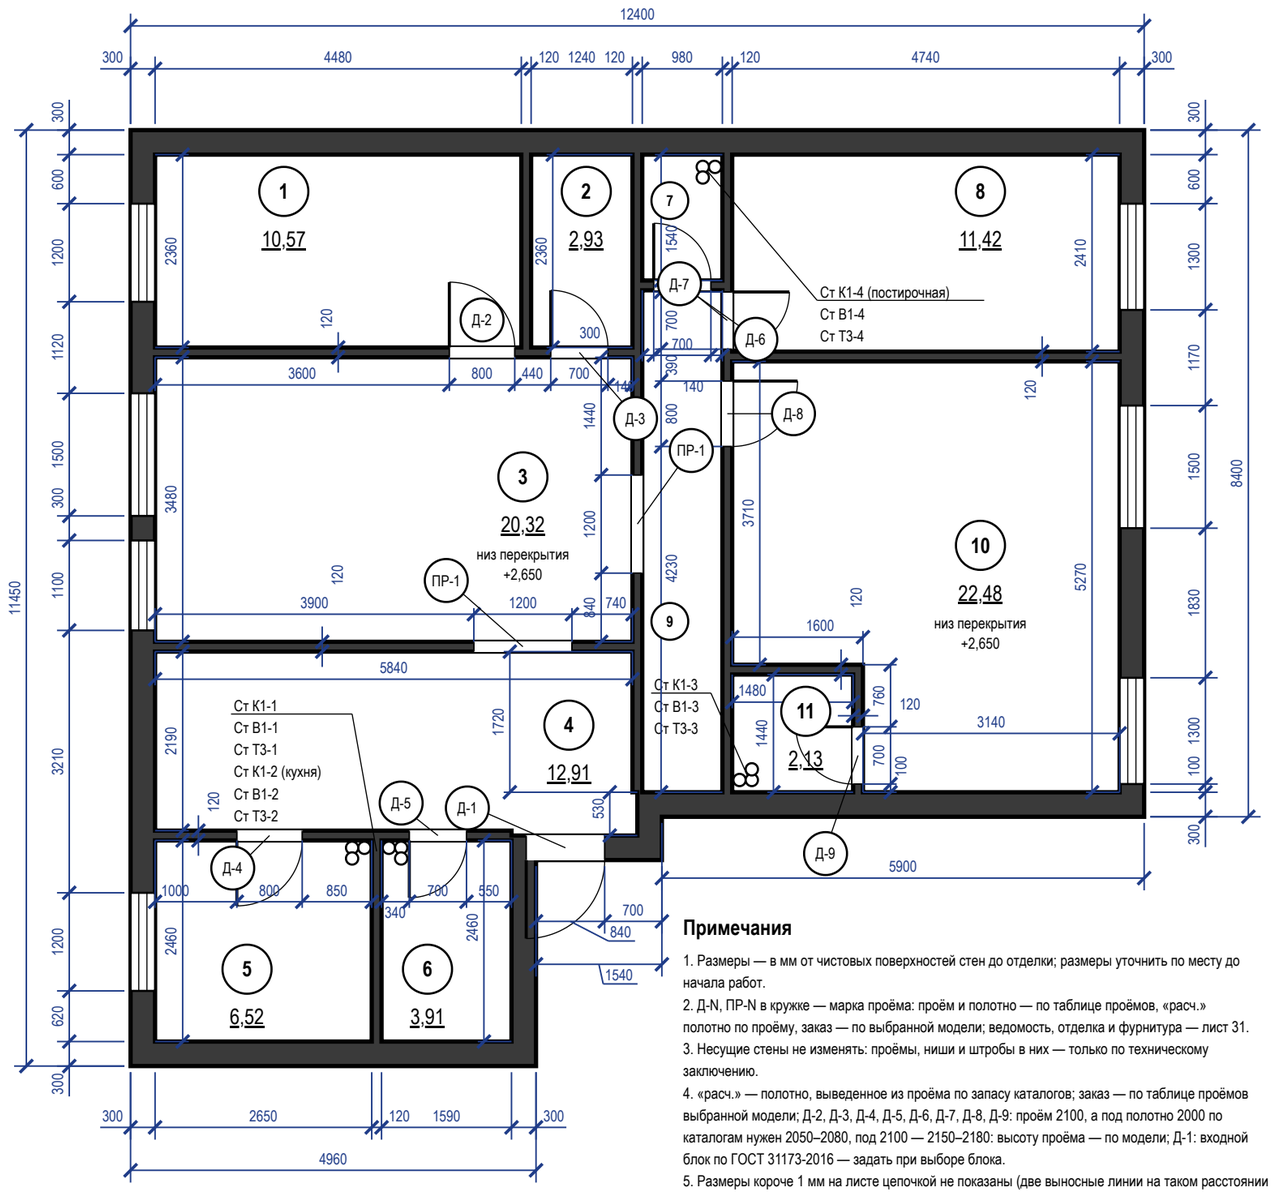

Экспликация помещений

№	Наименование	Площадь, м²
1	Кабинет-библиотека	10,57
2	Кладовая	2,93
3	Гостиная-столовая	20,32
4	Прихожая-холл	12,91
5	Кухня	6,52
6	Ванная	3,91
7	Постирочная	1,51
8	Спальня 2	11,42
9	Коридор	6,02
10	Спальня мастер	22,48
11	Ванная мастер	2,13
	Итого (общая площадь)	**100,72**

Таблица проёмов


Марка	Наименование	Проём ш×в, мм	Полотно (расч.)
Д-1	Дверь входная	960×2100	блок — задать
Д-2	Дверь скрытого монтажа	800×2100	700×2000
Д-3	Дверь скрытого монтажа	700×2100	600×2000
Д-4	Дверь скрытого монтажа	800×2100	700×2000
Д-5	Дверь скрытого монтажа	700×2100	600×2000
Д-6	Дверь скрытого монтажа	700×2100	600×2000
Д-7	Дверь скрытого монтажа	700×2100	600×2000
Д-8	Дверь скрытого монтажа	800×2100	700×2000
Д-9	Дверь скрытого монтажа	700×2100	600×2000
ПР-1	Проём без заполнения	1200×2100	

Примечания


1. Размеры — в мм от чистовых поверхностей стен до отделки; размеры уточнить по месту до начала работ.
2. Д-N, ПР-N в кружке — марка проёма: проём и полотно — по таблице проёмов, «расч.» полотно по проёму, заказ — по выбранной модели; ведомость, отделка и фурнитура — лист 31.
3. Несущие стены не изменять: проёмы, ниши и штробы в них — только по техническому заключению.
4. «расч.» — полотно, выведенное из проёма по запасу каталогов; заказ — по таблице проёмов выбранной модели; Д-2, Д-3, Д-4, Д-5, Д-6, Д-7, Д-8, Д-9: проём 2100, а под полотно 2000 по каталогам нужен 2050–2080, под 2100 — 2150–2180: высоту проёма — по модели; Д-1: входной блок по ГОСТ 31173-2016 — задать при выборе блока.
5. Размеры короче 1 мм на листе цепочкой не показаны (две выносные линии на таком расстоянии сливаются): пом. 9, стена Б — 20 мм от угла до проёма.

					Проект: Квартира 103 м²	**М 1:75**
	Лист	№ док.	Подпись	Дата	План монтажный	Стадия / Лист / Листов
Дизайнер	Кырлан А.С.			04.11.26		П / 6 / 96

Привязка выводов и крепление модулей

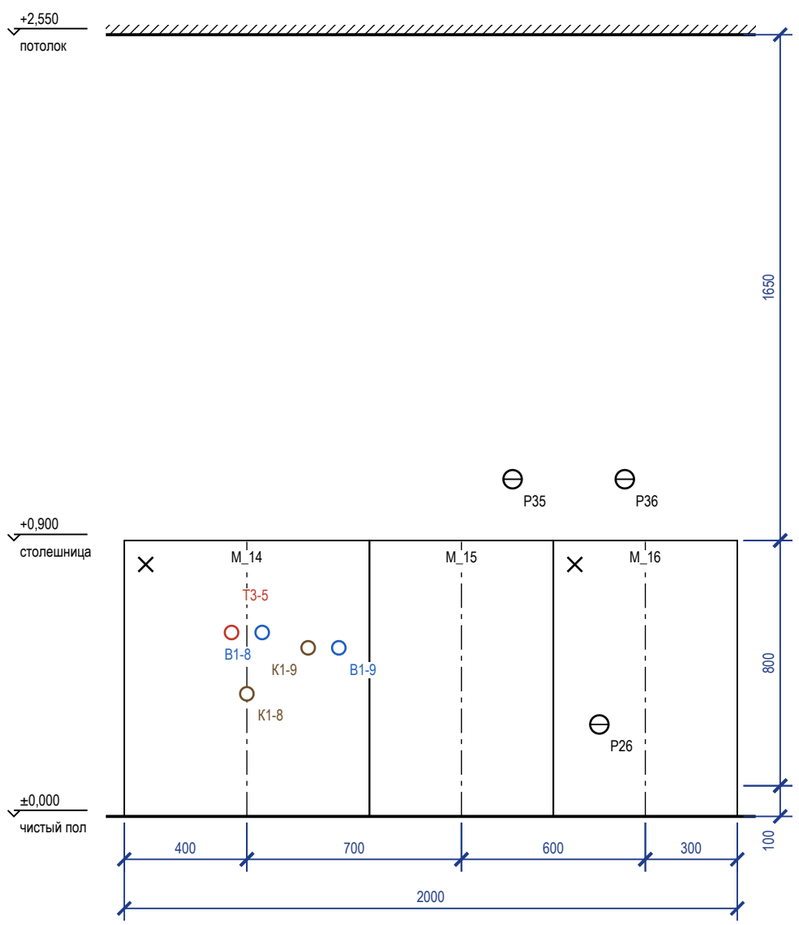

План столешницы

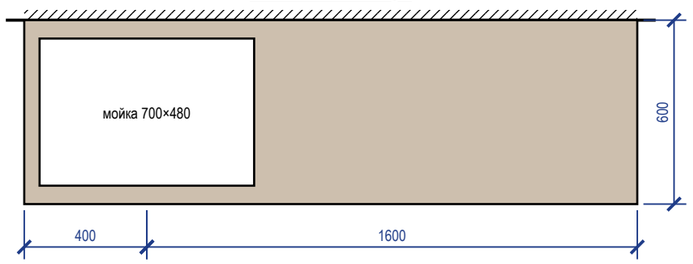

Привязка выводов к осям модулей

Код	Назначение	Модуль	От оси, мм	H, мм	Размещение
T3-5	T3 — межос. 100	M_14	−50	600	в модуле мойки
K1-8	K1 Ø50 — мойка	M_14	0	400	в модуле мойки
B1-8	B1 — межос. 100	M_14	+50	600	в модуле мойки
K1-9	K1 Ø40 — слив ПММ в шкафу мойки	M_14	+200	550	в модуле мойки
B1-9	B1 — кран ПММ в шкафу мойки	M_14	+300	550	в модуле мойки
P35	розетка ×2 — фартук	M_15	+167	1100	над столешницей (фартук)
P26	розетка — посудомоечная машина — в соседнем модуле, за ящиком	M_16	−150	300	в соседнем модуле, за ящиком
P36	розетка ×2 — фартук	M_16	−67	1100	над столешницей (фартук)

Зазоры под отделку

Поверхность	Отделка	Зазор, мм	Учесть
фартук	керамогранит	10	от чернового основания до корпуса навесных и столешницы
стены	окраска	5	под штукатурку и шпаклёвку за пеналом
пол	инженерная доска		цоколь — после укладки пола, опоры ±20 мм

Условные обозначения

- нижний модуль, пенал (контур)
- ось модуля (от неё — привязка вывода)
- анкер / уголок крепления к стене
- розетка на стене
- вывод кабеля к технике
- B1 — вывод воды B1 / T3, канализации K1


Примечания

1. Выводы — по проекту электрики и ВК; привязка по горизонтали — от оси модуля (плюс — вправо по виду), по высоте — от чистого пола до оси вывода.
2. Пенал — уголки к стене 2 шт. сверху; нижние модули — стяжками между собой и уголком к стене; ряд выставить по уровню опорами цоколя.
3. Розетки над столешницей — не ниже 150 мм над ней и не за корпусом техники; розетка за ПММ, духовым шкафом и холодильником — только в соседнем модуле или в зоне цоколя с доступом.
4. Столешница — вырезы по шаблонам выбранных моделей мойки и варочной панели; торцы у стены — герметик, пристеночный плинтус.


					Проект: Квартира 103 м²	M 1:20
	Лист	№ док.	Подпись	Дата		
Дизайнер	Кырлан А.С.			04.11.26	Кухня (пом. 5). Монтажная схема	Стадия: П; Лист: 7; Листов: 96

выпуск 04.11.2026 № d6a6e5e88d · стр. 7 из 96

Привязка выводов и крепление модулей

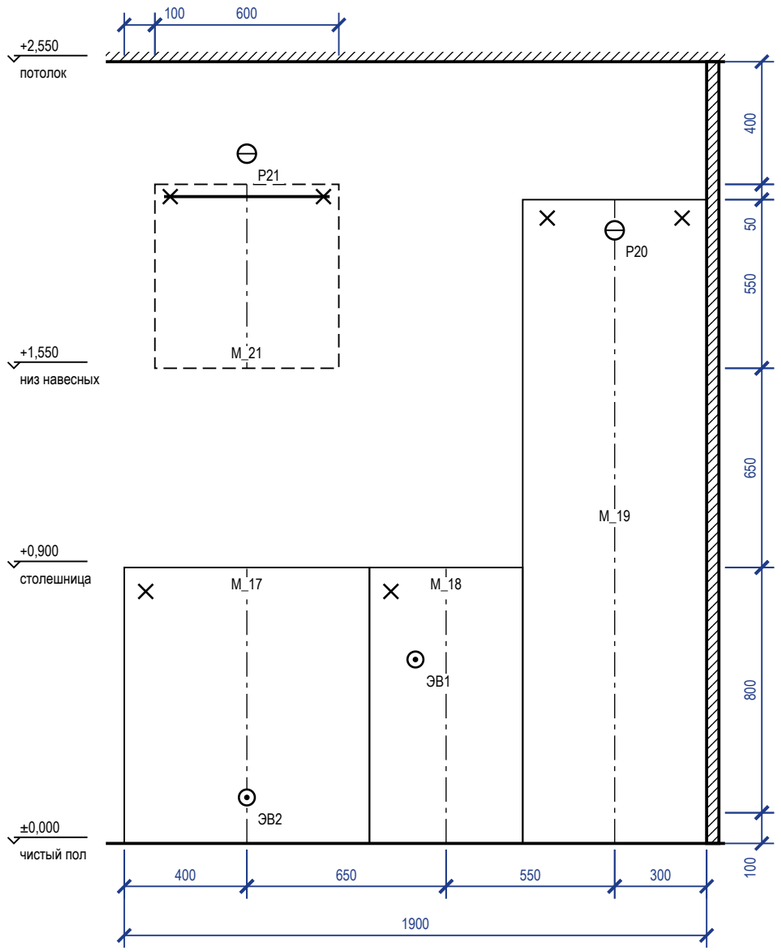

План столешницы

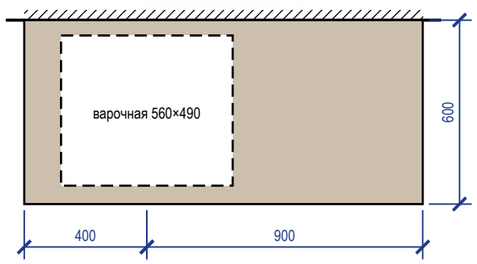

Привязка выводов к осям модулей

Код	Назначение	Модуль	От оси, мм	H, мм	Размещение
ЭВ2	вывод кабеля — духовой шкаф — в цоколе	M_17	0	150	под духовым шкафом, доступ через ящик
P21	розетка — вытяжка — над корпусом	M_21	0	2250	в навесном модуле
ЭВ1	вывод кабеля — варочная панель — в соседнем модуле, за ящиком	M_18	−100	600	в соседнем модуле, за ящиком
P20	розетка — холодильник — над нишей, съёмная панель	M_19	0	2000	над нишей холодильника, съёмная панель

Зазоры под отделку

Поверхность	Отделка	Зазор, мм	Учесть
фартук	керамогранит	10	от чернового основания до корпуса навесных и столешницы
стены	окраска	5	под штукатурку и шпаклёвку за пеналом
пол	инженерная доска		цоколь — после укладки пола, опоры ±20 мм

Условные обозначения


- нижний модуль, пенал (контур)
- невидимый контур: навесной модуль, корпус под столешницей
- ось модуля (от неё — привязка вывода)
- анкер / уголок крепления к стене
- розетка на стене
- вывод кабеля к технике
- B1 — вывод воды B1 / Т3, канализации К1

Примечания


1. Выводы — по проекту электрики и ВК; привязка по горизонтали — от оси модуля (плюс — вправо по виду), по высоте — от чистого пола до оси вывода.
2. Пенал — уголки к стене 2 шт. сверху; нижние модули — стяжками между собой и уголком к стене; ряд выставить по уровню опорами цоколя.
3. Розетки над столешницей — не ниже 150 мм над ней и не за корпусом техники; розетка за ПММ, духовым шкафом и холодильником — только в соседнем модуле или в зоне цоколя с доступом.
4. Столешница — вырезы по шаблонам выбранных моделей мойки и варочной панели; торцы у стены — герметик, пристеночный плинтус.

					Проект: Квартира 103 м²	M 1:20
	Лист	№ док.	Подпись	Дата		
Дизайнер	Кырлан А.С.			04.11.26	Кухня (пом. 5). Монтажная схема	Стадия: П; Лист: 8; Листов: 96


Система хранения M_05 (пом. 2)

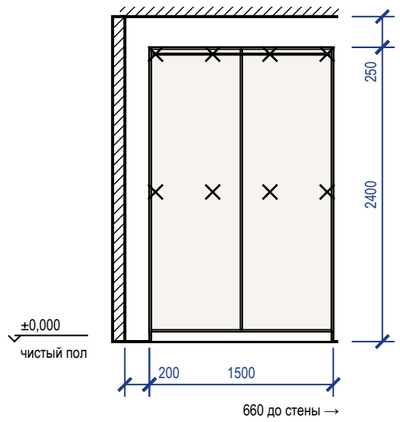


Шкаф-купе M_11 (пом. 4)

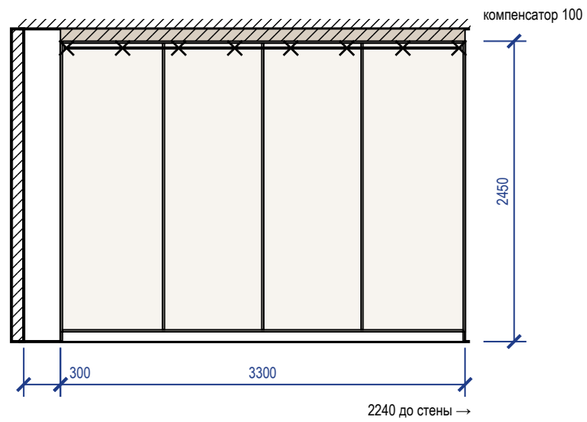


Система хранения M_22 пом. 7

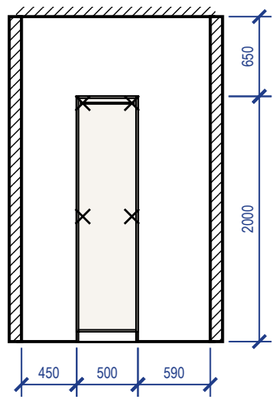

Шкаф распашной M_24 (пом. 8)

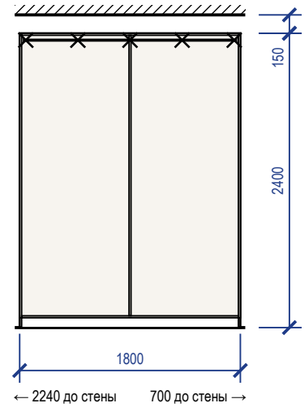

Шкаф распашной M_29 (пом. 10)

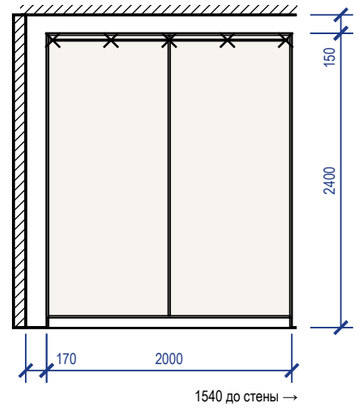

Крепление и зазоры под отделку

Марка	Помещение, стена	Основание	Отделка стены	Зазор, мм	Крепёж по планке	От опрокидывания
M_05	Кладовая (2), стена Б	по основанию — см. таблицу крепежа	окраска	5	анкер 8 шт. (2 ряда)	уголки 2 шт.
M_11	Прихожая-холл (4), стена А	по основанию — см. таблицу крепежа	окраска	5	анкер 8 шт., шаг 457	уголки 2 шт.
M_22	Постирочная (7), стена Б	по основанию — см. таблицу крепежа	окраска	5	анкер 4 шт. (2 ряда)	уголки 2 шт.
M_24	Спальня 2 (8), стена А	по основанию — см. таблицу крепежа	окраска	5	анкер 5 шт., шаг 425	уголки 2 шт.
M_29	Спальня мастер (10), стена Г	по основанию — см. таблицу крепежа	окраска	5	анкер 5 шт., шаг 475	уголки 2 шт.

Крепёж по основанию стены

Основание стены	Крепёж
бетон, ж/б	анкер-шуруп 7,5×72 или дюбель 8×60 с шурупом 5×70
кирпич полнотелый	дюбель 8×80 с шурупом 5×90
газобетон, пазогребень	дюбель для газобетона 10×100 или химический анкер
гипсокартон	закладная до обшивки (брус 40×80 или фанера 18 мм), саморез в закладную


Условные обозначения

- анкер / уголок крепления к стене
- корпус и полки ЛДСП (вид на стену)
- компенсатор — короб до потолка

Примечания

1. Установочные размеры — от чистого пола и чистых стен; перед установкой контрольный замер после отделки.
2. Порядок: корпус выставить по уровню опорами цоколя → закрепить к стене по задней планке → навесить двери и фасады, отрегулировать зазоры → подогнать и закрепить компенсатор.
3. Анкеры — с шагом не более 500 мм, не ближе 50 мм от края планки; на ГКЛ только в закладную, установленную до обшивки.
4. Скрытые коммуникации под анкеры проверить детектором; трассы электрики по плану розеток.

					Проект: Квартира 103 м²	**M 1:50**
	Лист	№ док.	Подпись	Дата	Шкафы. Монтажная схема	Стадия / Лист / Листов
Дизайнер	Кырлан А.С.			04.11.26		П / 9 / 96

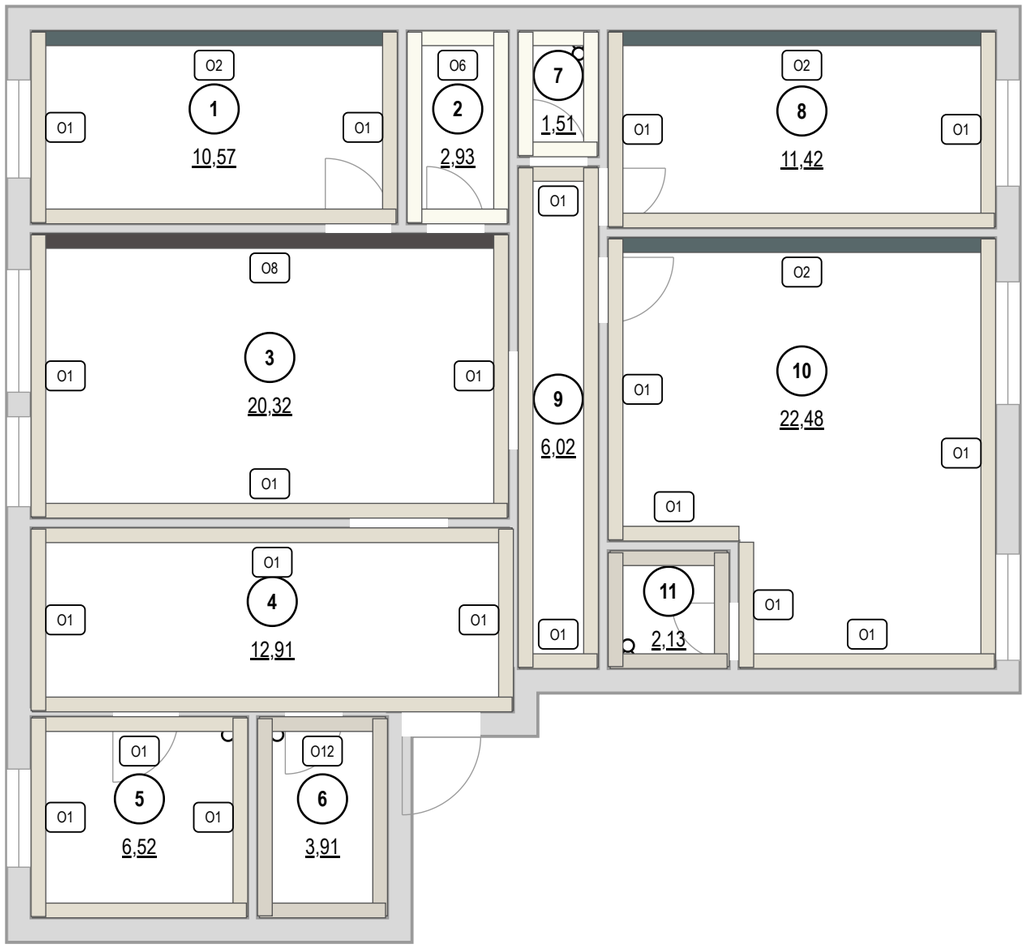

Покрытия стен

Марка	Покрытие	Помещение: S, м²	Итого, м²
O1	окраска Farrow & Ball · No. 291 «School House White — тёплый меловой белый»	1: 20,4; 3: 23,7; 4: 33,6; 5: 20,2; 8: 20,9; 9: 28,9; 10: 31,7	179,3
O2	окраска Farrow & Ball · No. 289 «Inchyra Blue — тёмный сине-серый»	1: 11,8; 8: 12,0; 10: 12,0	35,8
O6	окраска Tikkurila · S 0502-Y «Белый с лёгкой желтизной»	2: 17,3; 7: 11,6	28,9
O8	окраска Farrow & Ball · No. 255 «Tanner's Brown — тёмный шоколад»	3: 11,7	11,7
O12	облицовка плиткой Atlas Concorde · A8UZ «Marvel Travertine» 600×1200 мм	6: 17,5; 11: 12,1	29,6

Площади — нетто, по развёрткам (за вычетом проёмов и фартука); высоты помещений — от чистого пола.

	Лист	№ док.	Подпись	Дата
Дизайнер	Кырлан А.С.			04.11.26

Проект: Квартира 103 м² — **М 1:75**

Карта покрытий стен

Стадия	Лист	Листов
П	10	96

выпуск 04.11.2026 № d6a6e5e88d · стр. 10 из 96

Колерная карта по помещениям

Помещение	Поверхность	Образец	Поз.	Система и код цвета	Производитель, линейка / материал, артикул	Блеск	Класс истирания	LRV	Площадь
1. Кабинет-библиотека 10,57 м²	стены		**K1**	Farrow & Ball No. 291	Farrow & Ball · Modern Emulsion	матовая	1	73	19,9 м²
	акцент А		**K2**	Farrow & Ball No. 289	Farrow & Ball · Modern Emulsion	матовая	1	13	11,4 м²
	потолок		**K3**	NCS S 0502-Y	Tikkurila · Anti-Reflex 2	глубокомат.	2	95	10,6 м²
	пол		**KM1**	по образцу	Coswick · Вековые традиции · арт. 1167-4250				10,6 м²
	плинтус		**K4**	Farrow & Ball No. 291	МДФ · в цвет Farrow & Ball			73	12,9 м
2. Кладовая 2,93 м²	стены		**K5**	NCS S 0502-Y	Tikkurila · Harmony	матовая	1	95	17,6 м²
	потолок		**K3**	NCS S 0502-Y	Tikkurila · Anti-Reflex 2	глубокомат.	2	95	2,9 м²
	пол		**KM1**	по образцу	Coswick · Вековые традиции · арт. 1167-4250				2,9 м²
	плинтус		**K6**	NCS S 0502-Y	МДФ · в цвет NCS			95	6,5 м
3. Гостиная-столовая 20,32 м²	стены		**K1**	Farrow & Ball No. 291	Farrow & Ball · Modern Emulsion	матовая	1	73	23,6 м²
	акцент А		**K7**	Farrow & Ball No. 255	Farrow & Ball · Modern Emulsion	матовая	1	7	11,7 м²
	потолок		**K1**	Farrow & Ball No. 291	Farrow & Ball · Modern Emulsion	матовая	1	73	20,3 м²
	пол		**KM1**	по образцу	Coswick · Вековые традиции · арт. 1167-4250				20,3 м²
	плинтус		**K8**	Farrow & Ball No. 291	МДФ · в цвет Farrow & Ball	полуглянц.	2	73	14,7 м
4. Прихожая-холл 12,91 м²	стены		**K1**	Farrow & Ball No. 291	Farrow & Ball · Modern Emulsion	матовая	1	73	33,9 м²
	потолок		**K3**	NCS S 0502-Y	Tikkurila · Anti-Reflex 2	глубокомат.	2	95	12,9 м²
	пол		**KM2**	Marvel Travertine	Atlas Concorde · арт. A8UZ				12,9 м²
	плинтус		**K4**	Farrow & Ball No. 291	МДФ · в цвет Farrow & Ball			73	12,6 м
5. Кухня 6,52 м²	стены		**K1**	Farrow & Ball No. 291	Farrow & Ball · Modern Emulsion	матовая	1	73	20,5 м²
	потолок		**K1**	Farrow & Ball No. 291	Farrow & Ball · Modern Emulsion	матовая	1	73	6,5 м²
	пол		**KM1**	по образцу	Coswick · Вековые традиции · арт. 1167-4250				6,5 м²
	плинтус		**K8**	Farrow & Ball No. 291	МДФ · в цвет Farrow & Ball	полуглянц.	2	73	9,4 м
	фартук		**KM3**	тон Paper F497 (тёплый белый)	керамогранит · аналог по хар.				2,0 м²

Схема квартиры: цвет стен и акценты (б/м)

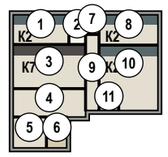


Схема палитры проекта

Стиль: Мид-сенчури 65% + Ар-деко 35% · схема: комплементарная

основной	основной	второстепенный	второстепенный	второстепенный	акцентный	акцентный	акцентный	акцентный
Farrow & Ball No. 291	NCS S 0502-Y	Farrow & Ball No. 298	Farrow & Ball No. 289	Farrow & Ball No. 255	NCS S 2050-Y20R	NCS S 3050-Y70R	NCS S 5030-B10G	NCS S 5040-B90G
School House White — тёплый меловой белый LRV 73 стены 1,3,4,5,8,9,10; плинтус 1,3,4,5,8,9,10; потолок 3,5; текстиль/декор 3	Белый с лёгкой желтизной LRV 95 потолок 1,2,4,6,7,8,9,10,11; стены 2,7; плинтус 2,7; текстиль/декор 1,8,10	Bancha — оливковый середины века LRV 14 текстиль/декор 3,10	Inchyra Blue — тёмный сине-серый LRV 13 акцент 1,8,10; текстиль/декор 1,8,10	Tanner's Brown — тёмный шоколад LRV 7 акцент 3; текстиль/декор 3	Горчичный LRV 42 текстиль/декор 1,8	Терракотовый / жжёный оранжевый LRV 18 текстиль/декор 1,8	Тил LRV 12 текстиль/декор 8	Изумрудный LRV 8 в отделке не применён

План 60/30/10



Окраска, факт — по площади стен, акцентов, потолков



окрашено всего 357 м²; второстепенный тон несут мебель и текстиль

Текстиль и декор в цветах вне палитры проекта

NCS S 1005-Y20R Светлый кремовый — пом. 1 (T7), 3 (T1, T4), 5 (T14), 8 (T11), 10 (T19, T22)

Условные обозначения

K1 Farrow & Ball No. 291 · School House White — тёплый меловой белый · Modern Emulsion · матовая · кл. 1

K2 Farrow & Ball No. 289 · Inchyra Blue — тёмный сине-серый · Modern Emulsion · матовая · кл. 1

K3 NCS S 0502-Y · Белый с лёгкой желтизной · Tikkurila Anti-Reflex 2 · глубокомат. · кл. 2

K4 Farrow & Ball No. 291 · School House White — тёплый меловой белый · МДФ

K5 NCS S 0502-Y · Белый с лёгкой желтизной · Tikkurila Harmony · матовая · кл. 1

K6 NCS S 0502-Y · Белый с лёгкой желтизной · МДФ

K7 Farrow & Ball No. 255 · Tanner's Brown — тёмный шоколад · Modern Emulsion · матовая · кл. 1

дерево (доска, паркет, ламинат) — рисунок досок

керамогранит, плитка, камень — сетка швов по формату

K8 Farrow & Ball No. 291 · School House White — тёплый меловой белый · МДФ · полуглянц. · кл. 2

K9 NCS S 0502-Y · Белый с лёгкой желтизной · Tikkurila Luja 7 · матовая · кл. 1

KM1 инженерная доска · 1167-4250

KM2 керамогранит · A8UZ

KM3 аналог: керамогранит матовый, тон F497, 600×600×9 мм

KM4 плитка · A8UZ

KM5 керамогранит · Atlas Concorde Marvel Travertine Sand
Cross 60×60 Matte Sensitech, арт. AFUL (той же коллекции, что стены A8UZ; тон сверить по образцу)

K — краска, KM — отделочный материал (тон KM — по описанию, эталон — образец материала); кл. — класс истирания (1 — самый стойкий к мытью);
LRV — светлота цвета: 0 — чёрный, 100 — белый

Примечания

1. Цвет на листе и на экране — ориентир. До покраски — выкрас на объекте: не меньше А3 (или лист ГКЛ), на грунте под эту краску, не на белой шпаклёвке, в 2 слоя; на обороте — код, бренд, веер, дата. Смотреть днём и вечером, рядом с образцами пола и плитки. Красить только в цвет утверждённого выкраса.
2. Краску заказывать по коду из графы «Система и код цвета» у бренда этого кода, не «аналогом» другого; весь объём одного кода — одной партией, колеруемую краску — за один проход машины.
3. Площади — те же, что в ведомости отделки (лист С1); сколько краски заказать — в спецификации отделочных материалов (лист С3).
4. Колерная карта на 2 листах: обозначения — на каждом, схема и палитра — на первом, выкрасы — на последнем.

					Проект: Квартира 103 м²
	Лист	№ док.	Подпись	Дата	
Дизайнер	Кырлан А.С.			04.11.26	Колерная карта
					Стадия: П; Лист: 11; Листов: 96

Колерная карта по помещениям (продолжение)

Помещение	Поверхность	Образец	Поз.	Система и код цвета	Производитель, линейка / материал, артикул	Блеск	Класс истирания	LRV	Площадь
6. Ванная 3,91 м²	стены		**KM4**	Marvel Travertine	Atlas Concorde · арт. A8UZ				18,0 м²
	потолок		**K9**	NCS S 0502-Y	Tikkurila · Luja 7	матовая	1	95	3,9 м²
	пол		**KM5**	по образцу	керамогранит · Atlas Concorde Marvel Travertine Sand Cross 60×60 Matte Sensitech, арт. AFUL (той же коллекции, что стены A8UZ; тон сверить по образцу)				3,9 м²
7. Постирочная 1,51 м²	стены		**K5**	NCS S 0502-Y	Tikkurila · Harmony	матовая	1	95	11,9 м²
	потолок		**K3**	NCS S 0502-Y	Tikkurila · Anti-Reflex 2	глубокомат.	2	95	1,5 м²
	пол		**KM1**	по образцу	Coswick · Вековые традиции · арт. 1167-4250				1,5 м²
	плинтус		**K6**	NCS S 0502-Y	МДФ · в цвет NCS			95	4,3 м
8. Спальня 2 11,42 м²	стены		**K1**	Farrow & Ball No. 291	Farrow & Ball · Modern Emulsion	матовая	1	73	20,9 м²
	акцент А		**K2**	Farrow & Ball No. 289	Farrow & Ball · Modern Emulsion	матовая	1	13	12,1 м²
	потолок		**K3**	NCS S 0502-Y	Tikkurila · Anti-Reflex 2	глубокомат.	2	95	11,4 м²
	пол		**KM1**	по образцу	Coswick · Вековые традиции · арт. 1167-4250				11,4 м²
	плинтус		**K4**	Farrow & Ball No. 291	МДФ · в цвет Farrow & Ball			73	13,6 м
9. Коридор 6,02 м²	стены		**K1**	Farrow & Ball No. 291	Farrow & Ball · Modern Emulsion	матовая	1	73	29,2 м²
	потолок		**K3**	NCS S 0502-Y	Tikkurila · Anti-Reflex 2	глубокомат.	2	95	6,0 м²
	пол		**KM1**	по образцу	Coswick · Вековые традиции · арт. 1167-4250				6,0 м²
	плинтус		**K4**	Farrow & Ball No. 291	МДФ · в цвет Farrow & Ball			73	10,8 м
10. Спальня мастер 22,48 м²	стены		**K1**	Farrow & Ball No. 291	Farrow & Ball · Modern Emulsion	матовая	1	73	31,5 м²
	акцент А		**K2**	Farrow & Ball No. 289	Farrow & Ball · Modern Emulsion	матовая	1	13	12,1 м²
	потолок		**K3**	NCS S 0502-Y	Tikkurila · Anti-Reflex 2	глубокомат.	2	95	22,5 м²
	пол		**KM1**	по образцу	Coswick · Вековые традиции · арт. 1167-4250				22,5 м²
	плинтус		**K4**	Farrow & Ball No. 291	МДФ · в цвет Farrow & Ball			73	18,5 м
11. Ванная мастер 2,13 м²	стены		**KM4**	Marvel Travertine	Atlas Concorde · арт. A8UZ				12,6 м²
	потолок		**K9**	NCS S 0502-Y	Tikkurila · Luja 7	матовая	1	95	2,1 м²
	пол		**KM5**	по образцу	керамогранит · Atlas Concorde Marvel Travertine Sand Cross 60×60 Matte Sensitech, арт. AFUL (той же коллекции, что стены A8UZ; тон сверить по образцу)				2,1 м²

Перечень выкрасов на согласование

№	Код	Бренд / веер	Пом. / стена	Подложка	Формат	Статус
1	No. 291	Farrow & Ball	1, 3, 4, 5, 8, 9, 10	ГКЛ с грунтом; МДФ под эмаль	600×1000; 300×600	к выполнению
2	No. 289	Farrow & Ball	1 А, 8 А, 10 А	ГКЛ с грунтом	600×1000	к выполнению
3	S 0502-Y	NCS Tikkurila	1, 2, 4, 6, 7, 8, 9, 10, 11	ГКЛ с грунтом; МДФ под эмаль	600×1000; 300×600	к выполнению
4	No. 255	Farrow & Ball	3 А	ГКЛ с грунтом	600×1000	к выполнению

Примечания

1. Цвет на листе и на экране — ориентир. До покраски — выкрас на объекте: не меньше А3 (или лист ГКЛ), на грунте под эту краску, не на белой шпаклёвке, в 2 слоя; на обороте — код, бренд, веер, дата. Смотреть днём и вечером, рядом с образцами пола и плитки; к основному цвету стен — ещё 2 соседних оттенка. Красить только в цвет утверждённого выкраса.
2. Краску заказывать по коду из графы «Система и код цвета» у бренда этого кода, не «аналогом» другого; весь объём одного кода — одной партией, колеруемую краску — за один проход машины.
3. Площади — те же, что в ведомости отделки (лист С1); сколько краски заказать — в спецификации отделочных материалов (лист С3).
4. Колерная карта на 2 листах: обозначения — на каждом, схема и палитра — на первом, выкрасы — на последнем.


Условные обозначения

- **K1** Farrow & Ball No. 291 · School House White — тёплый меловой белый · Modern Emulsion · матовая · кл. 1
- **K2** Farrow & Ball No. 289 · Inchyra Blue — тёмный сине-серый · Modern Emulsion · матовая · кл. 1
- **K3** NCS S 0502-Y · Белый с лёгкой желтизной · Tikkurila Anti-Reflex 2 · глубокомат. · кл. 2
- **K4** Farrow & Ball No. 291 · School House White — тёплый меловой белый · МДФ
- **K5** NCS S 0502-Y · Белый с лёгкой желтизной · Tikkurila Harmony · матовая · кл. 1
- **K6** NCS S 0502-Y · Белый с лёгкой желтизной · МДФ
- **K7** Farrow & Ball No. 255 · Tanner's Brown — тёмный шоколад · Modern Emulsion · матовая · кл. 1
- дерево (доска, паркет, ламинат) — рисунок досок
- керамогранит, плитка, камень — сетка швов по формату
- **K8** Farrow & Ball No. 291 · School House White — тёплый меловой белый · МДФ · полуглянц. · кл. 2
- **K9** NCS S 0502-Y · Белый с лёгкой желтизной · Tikkurila Luja 7 · матовая · кл. 1
- **KM1** инженерная доска · 1167-4250
- **KM2** керамогранит · A8UZ
- **KM3** аналог: керамогранит матовый, тон F497, 600×600×9 мм
- **KM4** плитка · A8UZ
- **KM5** керамогранит · Atlas Concorde Marvel Travertine Sand Cross 60×60 Matte Sensitech, арт. AFUL (той же коллекции, что стены A8UZ; тон сверить по образцу)

К — краска, КМ — отделочный материал (тон КМ — по описанию, эталон — образец материала); кл. — класс истирания (1 — самый стойкий к мытью); LRV — светлота цвета: 0 — чёрный, 100 — белый

					Проект: Квартира 103 м²
	Лист	№ док.	Подпись	Дата	
Дизайнер	Кырлан А.С.			04.11.26	Колерная карта

Стадия	Лист	Листов
П	12	96

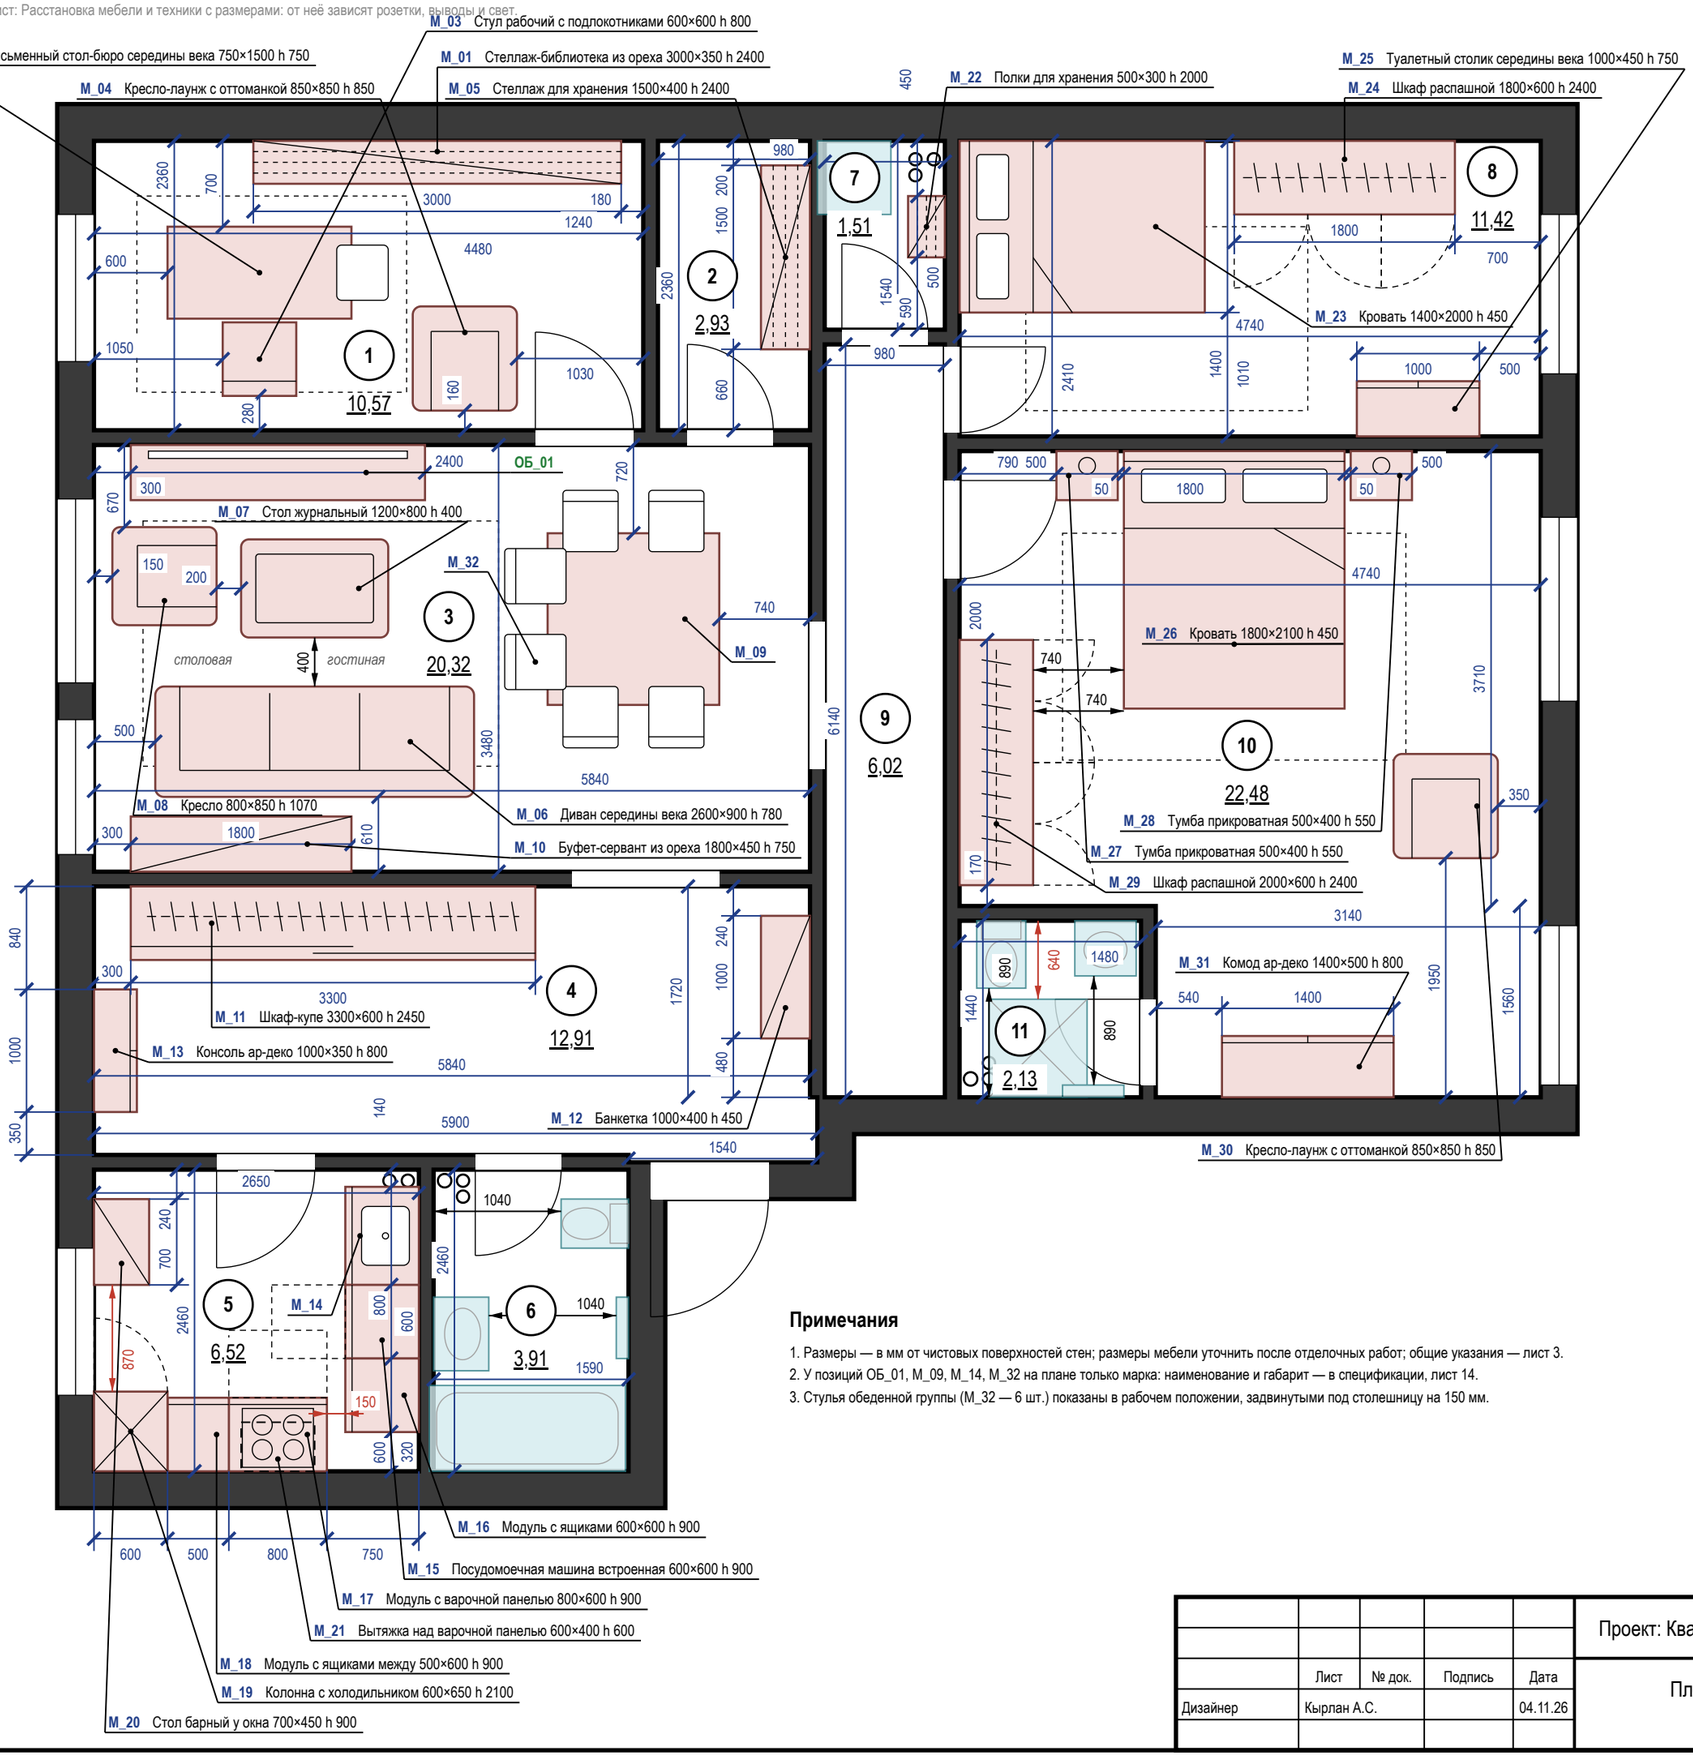

Экспликация помещений

лист 5 · на плане — номера в марках

Ведомость мебели и оборудования

Марка	Наименование	Ш×Г×В, мм	Пом.	Кол.
M_01	Стеллаж-библиотека из ореха	3000×350×2400	1	1
M_02	Письменный стол-бюро середины века	750×1500×750	1	1
M_03	Стул рабочий с подлокотниками	600×600×800	1	1
M_04	Кресло-лаунж с оттоманкой	850×850×850	1	1
M_05	Стеллаж для хранения	1500×400×2400	2	1
ОБ_01	ТВ-консоль из ореха	2400×450×550	3	1
M_06	Диван середины века	2600×900×780	3	1
M_07	Стол журнальный	1200×800×400	3	1
M_08	Кресло	800×850×1070	3	1
M_09	Стол обеденный на одной ножке	1400×1400×730	3	1
M_10	Буфет-сервант из ореха	1800×450×750	3	1
M_11	Шкаф-купе	3300×600×2450	4	1
M_12	Банкетка	1000×400×450	4	1
M_13	Консоль ар-деко	1000×350×800	4	1
M_14	Модуль под мойку	800×600×900	5	1
M_15	Посудомоечная машина встроенная	600×600×900	5	1
M_16	Модуль с ящиками	600×600×900	5	1
M_17	Модуль с варочной панелью	800×600×900	5	1
M_18	Модуль с ящиками между	500×600×900	5	1
M_19	Колонна с холодильником	600×650×2100	5	1
M_20	Стол барный у окна	700×450×900	5	1
M_21	Вытяжка над варочной панелью	600×400×600	5	1
M_22	Полки для хранения	500×300×2000	7	1
M_23	Кровать 1400×2000	1400×2000×450	8	1
M_24	Шкаф распашной	1800×600×2400	8	1
M_25	Туалетный столик середины века	1000×450×750	8	1
M_26	Кровать 1800×2100	1800×2100×450	10	1
M_27	Тумба прикроватная	500×400×550	10	1
M_28	Тумба прикроватная	500×400×550	10	1
M_29	Шкаф распашной	2000×600×2400	10	1
M_30	Кресло-лаунж с оттоманкой	850×850×850	10	1
M_31	Комод ар-деко	1400×500×800	10	1
M_32	Стул обеденный к столу M_09	450×500×820	3	6

Ш — вдоль стены (изголовья), Г — от стены (длина кровати)

Материалы, модели, допуск замены — лист 14

Примечания

1. Размеры — в мм от чистовых поверхностей стен; размеры мебели уточнить после отделочных работ; общие указания — лист 3.
2. У позиций ОБ_01, M_09, M_14, M_32 на плане только марка: наименование и габарит — в спецификации, лист 14.
3. Стулья обеденной группы (M_32 — 6 шт.) показаны в рабочем положении, задвинутыми под столешницу на 150 мм.

					Проект: Квартира 103 м²	М 1:50
	Лист	№ док.	Подпись	Дата	План размещения мебели и оборудования	
Дизайнер	Кырлан А.С.			04.11.26	Стадия: П	Лист: 13 / Листов: 96

Поз.	Наименование и техническая характеристика	Тип, марка, обозначение документа, опросного листа	Код продукции	Поставщик	Ед. измерения	Кол.	Масса 1 ед., кг	Примечание
	Мебель встроенная и корпусная (изготовление по чертежам мебельщика)							
M_05	Стеллаж для хранения; каркас и полки — ЛДСП декор «орех» 16 мм; без фасадов; Ш×Г×В 1500×400×2400 мм			изготовление на заказ	шт.	1		пом. 2
M_11	Шкаф-купе; корпус ЛДСП 16 мм; фасады — МДФ, шпон ореха 10 мм, масло матовое в профиле: латунь; Ш×Г×В 3300×600×2450 мм			изготовление на заказ	шт.	1		пом. 4
M_14	Модуль под мойку; корпус ЛДСП 16 мм; фасады — МДФ, шпон ореха 18 мм, масло матовое; Ш×Г×В 800×600×900 мм			изготовление на заказ	шт.	1		пом. 5
M_15	Модуль под встраиваемую ПММ 60; без корпуса (ниша между соседними модулями); фасад на дверь машины — МДФ 18 мм, эмаль матовая; цоколь; цвет фасадов — в цвет стен (Farrow & Ball No. 291); Ш×Г×В 600×600×900 мм			изготовление на заказ	шт.	1		пом. 5
M_16	Модуль с ящиками; корпус ЛДСП 16 мм; фасады — МДФ 18 мм, эмаль матовая; цвет фасадов — в цвет стен (Farrow & Ball No. 291); Ш×Г×В 600×600×900 мм			изготовление на заказ	шт.	1		пом. 5
M_17	Модуль с варочной панелью (индукция) и духовым шкафом; корпус ЛДСП 16 мм; фасады — МДФ 18 мм, эмаль матовая; цвет фасадов — в цвет стен (Farrow & Ball No. 291); Ш×Г×В 800×600×900 мм			изготовление на заказ	шт.	1		пом. 5
M_18	Модуль с ящиками между колонной и плитой; корпус ЛДСП 16 мм; фасады — МДФ 18 мм, эмаль матовая; цвет фасадов — в цвет стен (Farrow & Ball No. 291); Ш×Г×В 500×600×900 мм			изготовление на заказ	шт.	1		пом. 5
M_19	Колонна с холодильником, ретро-фасад; корпус ЛДСП 16 мм; фасады — МДФ эмаль 18 мм, матовая; цвет — тил; Ш×Г×В 600×650×2100 мм			изготовление на заказ	шт.	1		пом. 5
M_21	Вытяжка над варочной панелью; корпус ЛДСП 16 мм; фасады — МДФ 18 мм, эмаль матовая; цвет фасадов — в цвет стен (Farrow & Ball No. 291); Ш×Г×В 600×400×600 мм			изготовление на заказ	шт.	1		пом. 5
M_22	Полки для хранения (стена Б, в стороне от короба стояков); каркас и полки — ЛДСП 16 мм, декор «дуб натуральный»; без фасадов; Ш×Г×В 500×300×2000 мм			изготовление на заказ	шт.	1		пом. 7
M_24	Шкаф распашной, латунные ручки; корпус ЛДСП 16 мм; фасады — МДФ, шпон ореха 18 мм, масло матовое; Ш×Г×В 1800×600×2400 мм			изготовление на заказ	шт.	1		пом. 8
M_29	Шкаф распашной; корпус ЛДСП 16 мм; фасады — МДФ, шпон ореха 18 мм, масло матовое; вставка — латунь; Ш×Г×В 2000×600×2400 мм			изготовление на заказ	шт.	1		пом. 10
	Мебель покупная							
M_01	Стеллаж-библиотека из ореха на всю стену, латунные полкодержатели; шпон, дуб натуральный, матовое масло; Ш×Г×В 3000×350×2400 мм			аналог по характеристикам	шт.	1		пом. 1; замена ≤ габарита
M_02	Письменный стол-бюро середины века, орех, конические ножки; шпон, дуб натуральный, матовое масло; Ш×Г×В 750×1500×750 мм			аналог по характеристикам	шт.	1		пом. 1; замена ≤ габарита
M_03	Стул рабочий с подлокотниками, гнутая фанера и кожа; обивка — ткань, цвет Farrow & Ball No. 298; каркас — дуб натуральный; Ш×Г×В 600×600×800 мм			аналог по характеристикам	шт.	1		пом. 1; замена ≤ габарита
M_04	Кресло-лаунж с оттоманкой (в духе Eames Lounge Chair), палисандровый шпон, чёрная кожа; обивка — ткань, цвет Farrow & Ball No. 298; Ш×Г×В 850×850×850 мм			аналог по характеристикам	шт.	1		пом. 1; замена ≤ габарита
M_06	Диван середины века (в духе Florence Knoll), букле горчичного цвета, латунные опоры; обивка — ткань, цвет Farrow & Ball No. 298; Ш×Г×В 2600×900×780 мм			аналог по характеристикам	шт.	1		пом. 3; замена ≤ габарита
M_07	Стол журнальный (в духе Noguchi Coffee Table), орех и стекло; шпон, дуб натуральный, матовое масло; Ш×Г×В 1200×800×400 мм			аналог по характеристикам	шт.	1		пом. 3; замена ≤ габарита
M_08	Кресло (в духе Egg Chair), изумрудный бархат; обивка — ткань, цвет Farrow & Ball No. 298; Ш×Г×В 800×850×1070 мм			аналог по характеристикам	шт.	1		пом. 3; замена ≤ габарита
M_09	Стол обеденный на одной ножке (в духе Tulip Table), мрамор Calacatta, d 1400; шпон, дуб натуральный, матовое масло; Ш×Г×В 1400×1400×730 мм			аналог по характеристикам	шт.	1		пом. 3; замена ≤ габарита
M_10	Буфет-сервант из ореха на конических ножках, раздвижные двери; шпон, дуб натуральный, матовое масло; Ш×Г×В 1800×450×750 мм			аналог по характеристикам	шт.	1		пом. 3; замена ≤ габарита
M_32	Стул обеденный к столу M_09; обивка — ткань, цвет Farrow & Ball No. 298; каркас — дуб натуральный; Ш×Г×В 450×500×820 мм			аналог по характеристикам	шт.	6		пом. 3; замена ≤ габарита
ОБ_01	ТВ-консоль из ореха на конических ножках, ТВ на стене; шпон, дуб натуральный, матовое масло; Ш×Г×В 2400×450×550 мм			аналог по характеристикам	шт.	1		пом. 3; замена ≤ габарита
M_12	Банкетка, изумрудный бархат, латунные ножки; Ш×Г×В 1000×400×450 мм			аналог по характеристикам	шт.	1		пом. 4; замена ≤ габарита
M_13	Консоль ар-деко, чёрный лак и латунь; шпон, дуб натуральный, матовое масло; Ш×Г×В 1000×350×800 мм			аналог по характеристикам	шт.	1		пом. 4; замена ≤ габарита

Примечания

1. Позиции мебели совпадают с марками на плане расстановки; размеры Ш×Г×В — Ш вдоль стены, Г от стены.
2. Размеры и привязки плана расстановки — в мм от чистовых поверхностей стен: слой штукатурки 20 мм по блоку и 5 мм шпаклёвки по ГКЛ учтён; привязки — от стен и углов помещения, а не от другой мебели.
3. План расстановки не является документацией для изготовления мебели. Встроенная и корпусная мебель изготавливается по чертежам мебельщика после контрольного обмера (после штукатурки); «стена в стену» — с зазором 10 мм с каждой стороны или с компенсаторами; графы «Тип, марка» и «Код продукции» для неё не заполняются (ГОСТ 21.110-2013).
4. Покупные изделия — аналог по характеристикам: заменять только на изделия не больше указанного габарита и того же материала и цвета.
5. Материал и цвет, не указанные в данных изделия, приняты по концепции: тон дерева — по полу, обивка — по вторичному цвету палитры; образцы согласовать до заказа.
6. Масса 1 ед. для изделий до 25 кг не указывается. Техника — по монтажным схемам изготовителя; выводы — по листам ЭОМ и ВК.

					Проект: Квартира 103 м²
	Лист	№ док.	Подпись	Дата	Спецификация мебели и оборудования
Дизайнер	Кырлан А.С.			04.11.26	Стадия: П; Лист: 14; Листов: 96

Поз.	Наименование и техническая характеристика	Тип, марка, обозначение документа, опросного листа	Код продукции	Поставщик	Ед. измерения	Кол.	Масса 1 ед., кг	Примечание
M_20	Стол барный у окна, терраццо; Ш×Г×В 700×450×900 мм			аналог по характеристикам	шт.	1		пом. 5; замена ≤ габарита
M_23	Кровать 1400×2000, изголовье с каннелюрами, бархат цвета тил; мягкое изголовье, обивка — ткань, цвет Farrow & Ball No. 298; Ш×Г×В 1400×2000×450 мм			аналог по характеристикам	шт.	1		пом. 8; замена ≤ габарита
M_25	Туалетный столик середины века с круглым зеркалом; шпон, дуб натуральный, матовое масло; Ш×Г×В 1000×450×750 мм			аналог по характеристикам	шт.	1		пом. 8; замена ≤ габарита
M_26	Кровать 1800×2100 с высоким изголовьем ар-деко, изумрудный бархат, латунный кант; мягкое изголовье, обивка ткань, цвет Farrow & Ball No. 298; Ш×Г×В 1800×2100×450 мм			аналог по характеристикам	шт.	1		пом. 10; замена ≤ габарита
M_27, M_28	Тумба прикроватная, орех и латунь; шпон, дуб натуральный, матовое масло; Ш×Г×В 500×400×550 мм			аналог по характеристикам	шт.	2		пом. 10; замена ≤ габарита
M_30	Кресло-лаунж с оттоманкой (в духе Eames Lounge Chair), коньячная кожа; обивка — ткань, цвет Farrow & Ball No. 298; Ш×Г×В 850×850×850 мм			аналог по характеристикам	шт.	1		пом. 10; замена ≤ габарита
M_31	Комод ар-деко, макассар и латунь; шпон, дуб натуральный, матовое масло; Ш×Г×В 1400×500×800 мм			аналог по характеристикам	шт.	1		пом. 10; замена ≤ габарита
	Техника встраиваемая и бытовая (покупные изделия), светильники под розетки							
	Посудомоечная машина встраиваемая, в модуле M_15; ниша 600 мм	аналог по характеристикам: полновстраиваемая 60 см под фасад, ниша 600 × 862 мм, навеска фасада в комплекте		по выбору заказчика до изготовления мебели	шт.	1		пом. 5; по схеме изготовителя
	Духовой шкаф встраиваемый, в модуле M_17	аналог по характеристикам: 60 см, лицевая панель 595 мм, ниша 560 × 600, глубина ≥ 550 мм, вентиляция за прибором		по выбору заказчика до изготовления мебели	шт.	1		пом. 5; по схеме изготовителя
	Варочная панель встраиваемая, индукционная, в модуле M_17	аналог по характеристикам: индукционная 60 см, вырез 560 × 490 мм по шаблону модели		по выбору заказчика до изготовления мебели	шт.	1		пом. 5; по схеме изготовителя
	Холодильник встраиваемый, в модуле M_19	аналог по характеристикам: полновстраиваемый под фасад, ниша 1780 × 560 × 550 мм, вентиляция решётка в цоколе, выход сверху		по выбору заказчика до изготовления мебели	шт.	1		пом. 5; по схеме изготовителя
	Вытяжка, в модуле M_21	аналог по характеристикам: производительность — по расчёту ОВ, шум ≤ 55 дБ(А)		по выбору заказчика до изготовления мебели	шт.	1		пом. 5; по схеме изготовителя
	Стиральная машина, место по листу ВК (ОБ_02); Ш×Г 600×600 мм	аналог по характеристикам: тип загрузки — по листу ВК, в плане 600 × 600 мм (ширина × глубина), по листу ВК		по выбору заказчика до изготовления мебели	шт.	1		пом. 7; по схеме изготовителя
	Торшер, у поз. M_10; абажур — ткань или опаловое стекло; лампа 2700 K			аналог по характеристикам	шт.	1		пом. 3; розетка Р3 (ЭОМ)
	Текстиль							
T7	Портьеры-волна; лён 100 %; цвет NCS S 1005-Y20R; карниз 1820 мм, высота 2640 мм, сборка 2			аналог по характеристикам	шт.	2		пом. 1
T8	Тюль; полиэстер 100 %; цвет NCS S 0502-Y; карниз 1820 мм, высота 2640 мм, сборка 2,5			аналог по характеристикам	шт.	1		пом. 1
T9	Ковёр под рабочей зоной, геометрия середины века; шерсть 100 %; цвет NCS S 2050-Y20R; 2200×1600 мм			аналог по характеристикам	шт.	1		пом. 1; с подложкой
T10	Подушки декоративные на кровать; букле (шерсть 60 %, полиэстер 40 %); цвет NCS S 3050-Y70R			аналог по характеристикам	шт.	3		пом. 1
T12	Плед на кровать; шерсть мериноса 100 %; цвет Farrow & Ball No. 289			аналог по характеристикам	шт.	1		пом. 1
T1	Портьеры-волна, два полотна; лён 100 %; цвет NCS S 1005-Y20R; карниз 2150 мм, высота 2640 мм, сборка 2			аналог по характеристикам	шт.	2		пом. 3
T2	Тюль-вуаль, одно полотно; полиэстер 100 %; цвет Farrow & Ball No. 291; карниз 2150 мм, высота 2640 мм, сборка 2,5			аналог по характеристикам	шт.	1		пом. 3
T3	Ковёр мягкой группы, абстрактная геометрия середины века; шерсть 100 %; цвет Farrow & Ball No. 298; 2900×2000 мм			аналог по характеристикам	шт.	1		пом. 3; с подложкой
T4	Подушки декоративные на диван; лён 100 %; цвет NCS S 1005-Y20R			аналог по характеристикам	шт.	3		пом. 3

Поз.	Наименование и техническая характеристика	Тип, марка, обозначение документа, опросного листа	Код продукции	Поставщик	Ед. измерения	Кол.	Масса 1 ед., кг	Примечание
Т5	Подушки декоративные на диван, акцент; хлопковый бархат 100 %; цвет Farrow & Ball No. 255			аналог по характеристикам	шт.	2		пом. 3
Т6	Плед на диван; шерсть мериноса 100 %; цвет Farrow & Ball No. 255			аналог по характеристикам	шт.	1		пом. 3
Т14	Рулонная штора кассетная, ткань димаут; полиэстер 100 %; цвет NCS S 1005-Y20R; карниз 1600 мм, высота 1750 мм			аналог по характеристикам	шт.	1		пом. 5
Т11	Портьеры-волна; лён 100 %; цвет NCS S 1005-Y20R; карниз 1820 мм, высота 2640 мм, сборка 2			аналог по характеристикам	шт.	2		пом. 8
Т13	Тюль; полиэстер 100 %; цвет NCS S 0502-Y; карниз 1820 мм, высота 2640 мм, сборка 2,5			аналог по характеристикам	шт.	1		пом. 8
Т15	Ковёр под кроватью; шерсть 100 %; цвет NCS S 2050-Y20R; 2300×1500 мм			аналог по характеристикам	шт.	1		пом. 8; с подложкой
Т16	Подушки декоративные на кровать; букле (шерсть 60 %, полиэстер 40 %); цвет NCS S 3050-Y70R			аналог по характеристикам	шт.	3		пом. 8
Т17	Подушки на кровать, акцент; хлопковый бархат 100 %; цвет NCS S 5030-B10G			аналог по характеристикам	шт.	2		пом. 8
Т18	Плед на кровать; шерсть мериноса 100 %; цвет Farrow & Ball No. 289			аналог по характеристикам	шт.	1		пом. 8
Т19	Портьеры-волна; лён 100 %; цвет NCS S 1005-Y20R; карниз 2500 мм, высота 2640 мм, сборка 2			аналог по характеристикам	шт.	2		пом. 10
Т20	Тюль; полиэстер 100 %; цвет NCS S 0502-Y; карниз 2500 мм, высота 2640 мм, сборка 2,5			аналог по характеристикам	шт.	1		пом. 10
Т21	Ковёр под кроватью; шерсть 80 %, хлопок 20 %; цвет Farrow & Ball No. 298; 2800×1850 мм			аналог по характеристикам	шт.	1		пом. 10; с подложкой
Т22	Подушки декоративные на кровать; лён 100 %; цвет NCS S 1005-Y20R			аналог по характеристикам	шт.	3		пом. 10
Т23	Подушки на кровать, акцент; хлопковый бархат 100 %; цвет Farrow & Ball No. 289			аналог по характеристикам	шт.	2		пом. 10
Т24	Плед на кровать; шерсть мериноса 100 %; цвет Farrow & Ball No. 289			аналог по характеристикам	шт.	1		пом. 10
	Декор							
ДК3	Картина над креслом: графика середины века, рама — орех; 1000×700 мм; низ на 1100 мм от пола			аналог по характеристикам	шт.	1	4	пом. 1; крепление к стене
ДК1	Картина над буфетом: абстракция середины века, рама — латунь; 1200×900 мм; низ на 1000 мм от пола			аналог по характеристикам	шт.	1	6	пом. 3; крепление: планка на дюбелях, 4 точки
ДК2	Фикус лировидный в кашпо Ø400; 450×450 мм			аналог по характеристикам	шт.	1		пом. 3
ДК5	Зеркало; рама — чёрный матовый; 800×1800 мм; низ на 550 мм от пола			аналог по характеристикам	шт.	1	18	пом. 4; крепление: анкер, 4 шт.
ДК8	Часы настенные Ø400; 400×400 мм; центр на 1550 мм от пола			аналог по характеристикам	шт.	1	2	пом. 5; крепление: дюбель с крюком, 1 точка
ДК9	Хлорофитум хохлатый на подоконнике (отм. +0,800); 300×200 мм; низ на 800 мм от пола			аналог по характеристикам	шт.	1		пом. 5
ДК4	Картина над кроватью: графика в паспарту, рама — дуб; 1000×700 мм; низ на 1100 мм от пола			аналог по характеристикам	шт.	1	4	пом. 8; крепление к стене
ДК6	Зеркало в рост в тонкой чёрной раме; рама — чёрный матовый; 600×1600 мм; низ на 300 мм от пола			аналог по характеристикам	шт.	1	12	пом. 8; крепление: анкер для пустотелых оснований, 4 шт.
ДК7	Картина над кроватью: абстракция, холст, тонкая рама из дуба; 1200×700 мм; низ на 1300 мм от пола			аналог по характеристикам	шт.	1	4	пом. 10; крепление к стене

					Проект: Квартира 103 м²		
	Лист	№ док.	Подпись	Дата	Спецификация мебели и оборудования (продолжение)	Стадия	Лист	Листов
Дизайнер	Кырлан А.С.			04.11.26		П	16	96

Ведомость изделий

Марка	Наименование	Пом.	Ш×Г×В, мм	Корпус	Фасад	Кромка, мм	Кол.
M_05	Система хранения	2	1500×400×2400	ЛДСП декор «орех» 16	без фасадов	0,4 / 2	1
M_11	Шкаф-купе	4	3300×600×2450	ЛДСП 16	МДФ, шпон ореха 10 мм, масло матовое в профиле: латунь	0,4 / 2	1
M_22	Система хранения	7	500×300×2000	ЛДСП 16	без фасадов	0,4 / 2	1
M_24	Шкаф распашной	8	1800×600×2400	ЛДСП 16	МДФ, шпон ореха 18 мм, масло матовое	0,4 / 2	1
M_29	Шкаф распашной	10	2000×600×2400	ЛДСП 16	МДФ, шпон ореха 18 мм, масло матовое; вставка — латунь	0,4 / 2	1
M_14	Модуль нижний: мойка	5	800×600×900	ЛДСП 16	МДФ, шпон ореха 18 мм, масло матовое	0,4 / 2	1
M_15	Модуль под ПММ 60: без корпуса, фасад на дверь машины	5	600×600×900	без корпуса	МДФ 18 мм, эмаль матовая — на дверь машины (навеска из её комплекта), цоколь		1
M_16	Модуль нижний: ящики	5	600×600×900	ЛДСП 16	МДФ 18 мм, эмаль матовая	0,4 / 2	1
M_17	Модуль нижний: духовой шкаф, варочная	5	800×600×900	ЛДСП 16	МДФ 18 мм, эмаль матовая	0,4 / 2	1
M_21	Модуль навесной: полки	5	600×400×600	ЛДСП 16	МДФ 18 мм, эмаль матовая	0,4 / 2	1
M_18	Модуль нижний: ящики	5	500×600×900	ЛДСП 16	МДФ 18 мм, эмаль матовая	0,4 / 2	1
M_19	Пенал: холодильник встр.	5	600×650×2100	ЛДСП 16	МДФ эмаль 18 мм, матовая; цвет — тип	0,4 / 2	1

Ведомость встраиваемой техники

Поз.	Прибор	Ниша, вырез, мм	Вентиляция	Питание	Схема
M_14	Мойка врезная / подстольная с сифоном	вырез по шаблону, ориентир 700 × 480		смеситель — выводы ВК	по модели
M_15	Посудомоечная машина встраиваемая, 60 см	ниша 600 × 862 (от пола до низа столешницы)	зазор в цоколе, по схеме	Р26: M_16, H=300 — в соседнем модуле, за ящиком	по модели
M_17	Духовой шкаф встраиваемый, 60 см	ниша 560 × 600, глубина ≥ 550	зазор за шкафом, вырез в задней стенке	ЭВ2: M_17, H=150 — под духовым шкафом, доступ через ящик	по модели
M_17	Варочная панель индукционная, 60 см	вырез в столешнице 560 × 490		ЭВ1: M_18, H=600 — в соседнем модуле, за ящиком	по модели
M_19	Холодильник встраиваемый, ниша 1780	ниша 1780 × 560 × 550	решётка в цоколе, канал за корпусом, выход сверху	Р20: M_19, H=2000 — над нишей холодильника, съёмная панель	по модели
M_21	Вытяжка встраиваемая в навесной модуль, 60 см	низ ≥ 650 над панелью	воздуховод к вентканалу, короб до потолка	Р21: M_21, H=2250 — в навесном модуле	по модели

Ведомость фурнитуры

№	Фурнитура	Тип, размер	Изделия	Кол.
1	Полкодержатель с фиксацией	ø5 мм	M_05, M_11, M_22, M_24, M_29, M_21, M_19	136
2	Штанга выдвижная торцевая	L по глубине	M_05	1
3	Опора регулируемая с цоколем на клипсах	ход 20 мм	M_05, M_11, M_22, M_24, M_29	38
4	Анкер по основанию стены	по таблице крепежа	M_05, M_11, M_22, M_24, M_29, M_21	32
5	Уголок крепления к стене от опрокидывания	стальной	M_05, M_11, M_22, M_24, M_29, M_19	12
6	Система дверей купе: профиль, направляющие, ролики	на 4 двери	M_11	1
7	Ручка-профиль вертикальная	в цвет профиля	M_11	4
8	Штанга овальная 30×15, L = 817	+ 2 держателя	M_11	1
9	Полка для обуви выдвижная наклонная	ширина 817	M_11	3
10	Полка для обуви выдвижная наклонная	ширина 794	M_11	3
11	Штанга овальная 30×15, L = 794	+ 2 держателя	M_11	1
12	Петля накладная 110° с доводчиком	чашка 35 мм	M_24, M_29, M_14, M_21, M_19	63
13	Штанга овальная 30×15, L = 876	+ 2 держателя	M_24	1
14	Штанга овальная 30×15, L = 976	+ 2 держателя	M_29	1
15	Ручка-профиль	латунь матовая	M_14, M_15, M_16, M_17, M_21, M_18, M_19	15
16	Опора кухонная регулируемая 100–120 мм	+ клипса цоколя	M_14, M_16, M_17, M_18, M_19	24
17	Комплект навески фасада ПММ	из поставки машины	M_15	1
18	Направляющие полного выдвижения с доводчиком NL 500	пара	M_16, M_17, M_18	7
19	Навес регулируемый для навесного шкафа	пара на секцию	M_21	1
20	Шина монтажная	L = 540	M_21	1


Примечания

1. Модели техники выбирает заказчик до изготовления мебели; ниши, вырезы и вентиляция — по монтажной схеме выбранной модели (условие гарантии), её номер вносится в ведомость.
2. Количество фурнитуры — по чертежам изделий; запас крепежа 5 %. Аналоги — по характеристикам (доводчик, нагрузка, ход).
3. Цвет корпусов, фасадов и профилей — по колерной карте проекта. Кромка — скрытые / видимые торцы, мм.


					Проект: Квартира 103 м²
	Лист	№ док.	Подпись	Дата	Ведомости изделий, техники и фурнитуры
Дизайнер	Кырлан А.С.			04.11.26	

Стадия	Лист	Листов
П	17	96


Фрагмент 1. Ванная (пом. 6)

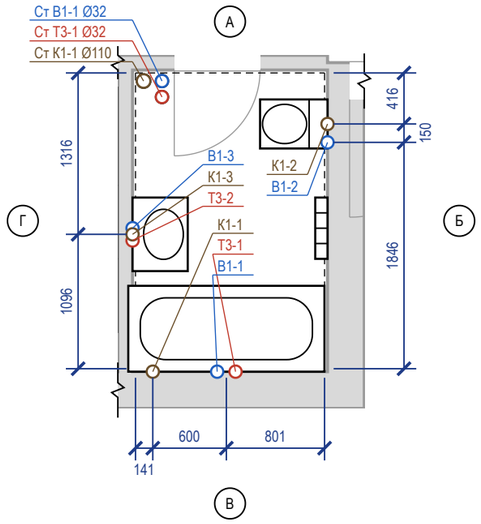


Фрагмент 2. Постирочная (пом. 7)

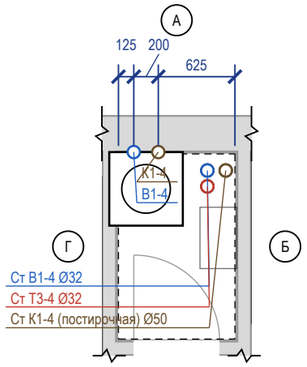

Фрагмент 3. Ванная мастер (пом. 11)

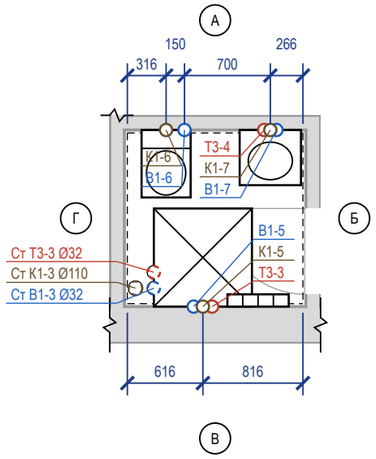

Фрагмент 4. Кухня (пом. 5)

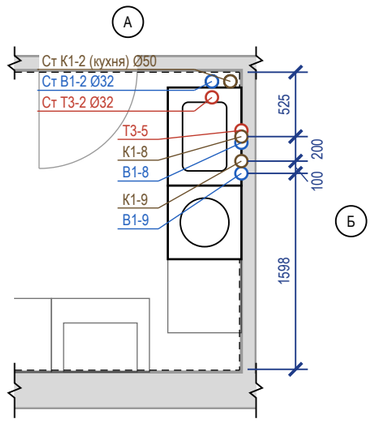

Ведомость привязок выводов

Код	Прибор	Ø	Н, мм	Привязка от чист. стен, мм	Прим.
В1-1	С_01 ванна	½"	800	ст. В: 666 от Г	межос. 150
Т3-1	С_01 ванна	½"	800	ст. В: 726 от Б	межос. 150
К1-1	С_01 ванна	Ø50	50	ст. В: 141 от Г	
В1-2	С_02 унитаз подвесной	½"	250	ст. Б: 566 от А	в раме инсталляции
К1-2	С_02 унитаз подвесной	Ø110	220	ст. Б: 416 от А	
В1-3	С_03 умывальник	½"	600	ст. Г: 1146 от В	межос. 100
Т3-2	С_03 умывальник	½"	600	ст. Г: 1046 от В	межос. 100
К1-3	С_03 умывальник	Ø50	500	ст. Г: 1096 от В	
В1-4	ОБ_02 стиральная машина	½"	600	ст. А: 125 от Г	кран машины
К1-4	ОБ_02 стиральная машина	Ø50	600	ст. А: 325 от Г	
В1-5	С_05 душ	½"	1200	ст. В: 541 от Г	межос. 150
Т3-3	С_05 душ	½"	1200	ст. В: 691 от Г	межос. 150
К1-5	С_05 душ	Ø50	70	ст. В: 616 от Г	сифон поддона
В1-6	С_06 унитаз подвесной	½"	250	ст. А: 466 от Г	в раме инсталляции
К1-6	С_06 унитаз подвесной	Ø110	220	ст. А: 316 от Г	
В1-7	С_07 умывальник	½"	600	ст. А: 216 от Б	межос. 100
Т3-4	С_07 умывальник	½"	600	ст. А: 316 от Б	межос. 100
К1-7	С_07 умывальник	Ø50	500	ст. А: 266 от Б	
В1-8	М_14 мойка кухонная	½"	600	ст. Б: 575 от А	межос. 100
Т3-5	М_14 мойка кухонная	½"	600	ст. Б: 475 от А	межос. 100
К1-8	М_14 мойка кухонная	Ø50	400	ст. Б: 525 от А	
В1-9	М_15 посудомоечная машина	½"	550	ст. Б: 825 от А	кран ПММ в шкафу мойки
К1-9	М_15 посудомоечная машина	Ø40	550	ст. Б: 725 от А	слив ПММ в шкафу мойки

Условные обозначения


- вывод В1 (код — в ведомости привязок)
- вывод Т3 (код — в ведомости привязок)
- вывод К1 (код — в ведомости привязок)
- сантехприбор по расстановке (габарит модели)
- чистовая поверхность стены (от неё привязки)
- стояк «Ст К1-N / Ст В1-N» (ГОСТ 21.601), Ø мм
- стояк Т3 не на обмере — принят в шахте рядом со Ст В1, сверить
- линия обрыва (граница фрагмента)
- А — обозначение стены А–Г (как на развёртках)

Примечания


1. Привязки выводов даны от чистовых поверхностей стен (облицовка на сторону: ванная — 24 мм (штукатурка 10 + клей 5 + плитка 9); постирочная — 15 мм (штукатурка 10 + шпаклёвка 5 (принято)); ванная мастер — 24 мм (штукатурка 10 + клей 5 + плитка 9); кухня — 22 мм (фартук: штукатурка 10 + клей 3 + плитка 9)); эти же грани — на развёртках и в раскладке плитки. Высоты — от чистого пола помещения.
2. До черновой разводки сверить по паспорту выбранного прибора (смеситель, инсталляция, сифон).
3. Горячая вода (Т3) — слева от холодной (В1), если смотреть на прибор. Допуск установки выводов: ±5 мм в группе, ±20 мм у отдельно стоящих.
4. Расчёт систем водоснабжения и канализации и подбор оборудования выполняет проектная организация; лист задаёт места и высоты выводов.
5. Посудомоечная машина М_15: кран и слив — отдельными выводами в шкафу мойки (не за машиной), до машины ≤ 1500 мм.
6. Прибор М_14 мойка кухонная, М_15 посудомоечная машина взят из расстановки мебели (по шкафу с мойкой).
7. Ст К1-3, Ст В1-3, Ст Т3-3 на обмере не показаны: положение принято, не замерено; положение сверить на объекте до разметки.
8. Стояки в коробах/шахтах не замоноличивать; стояк К1 в коробе — звукоизоляция стояка в коробе без жёсткого контакта с трубой; к арматуре и ревизиям — люк не меньше 300×400.

					Проект: Квартира 103 м² — М 1:50
	Лист	№ док.	Подпись	Дата	План выводов сантехники
Дизайнер	Кырлан А.С.			04.11.26	Стадия: П; Лист: 18; Листов: 96

План квартиры (М 1:200)

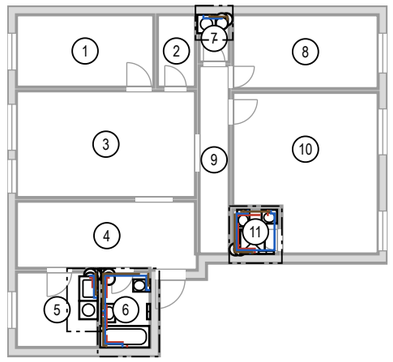


Фр. 2. Постирочная (М 1:25)

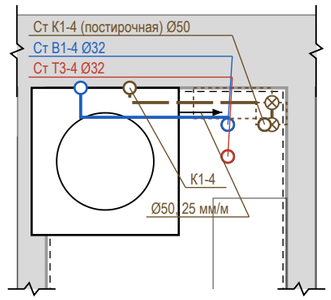


Условные обозначения

- В1 — водопровод хозяйственно-питьевой (ХВС), PP-R Ø20
- Т3 — горячее водоснабжение, подача (ГВС), PP-R Ø20
- К1 — канализация бытовая
- направление уклона К1 / пола: Ø, мм на 1 м
- ревизия (прочистка) К1 — доступ сохранить
- тройник (ответвление к прибору)
- короб К1 над чистым полом (ГКЛВ под плитку)
- вывод В1 (код — в ведомости привязок)
- вывод Т3 (код — в ведомости привязок)
- вывод К1 (код — в ведомости привязок)
- сантехприбор по расстановке (габарит модели)
- стояк «Ст К1-N / Ст В1-N» (ГОСТ 21.601), Ø мм
- стояк Т3 не на обмере — принят в шахте рядом со Ст В1, сверить
- линия обрыва (граница фрагмента)
- граница фрагмента на плане (Фр. N)


Фр. 1. Ванная (М 1:25)

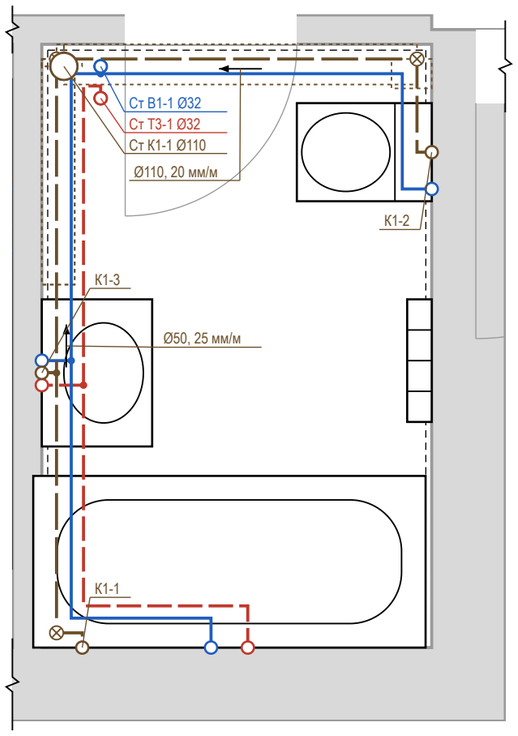

Фр. 3. Ванная мастер (М 1:25)

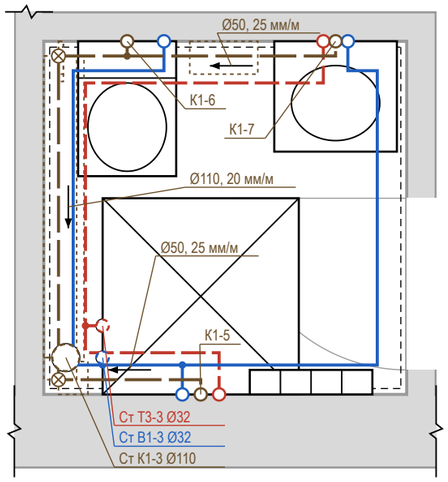

Фр. 4. Кухня (М 1:25)

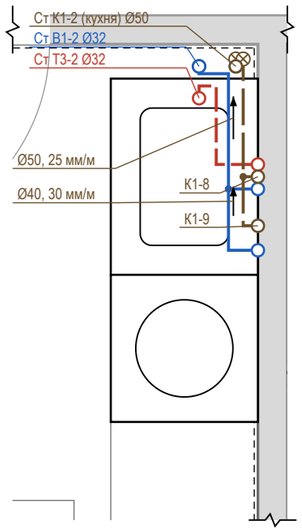


Профиль выпусков К1 (до врезки в стояк)

Выпуск	Прибор	Ø	L, м	i, мм/м	Δh, мм	Прокладка, мм
К1-2	С_02 унитаз подвесной	Ø110	1,91	20	38	под проёмом Д-5: короба нет; до решения
К1-6	С_06 унитаз подвесной	Ø110	1,60	20	32	короб 180×140
К1-1	С_01 ванна	Ø50	2,56	25	64	короб 150×110
К1-7	С_07 умывальник	Ø50	2,45	25	61	короб 150×110
К1-3	С_03 умывальник	Ø50	1,40	25	35	короб 120×110
К1-4	ОБ_02 стиральная машина	Ø50	0,76	25	19	короб 100×110
К1-5	С_05 душ	Ø50	0,76	25	19	короб 100×110
К1-8	М_14 мойка кухонная	Ø50	0,60	25	15	над полом за приборами
К1-9	М_15 посудомоечная машина	Ø40	0,80	30	24	над полом за приборами

Короб h×b: h — от чистого пола, b — от чистовой стены. Стяжка 35 мм — лист полов.

Узел ввода В1, Т3 (схема, без масштаба)

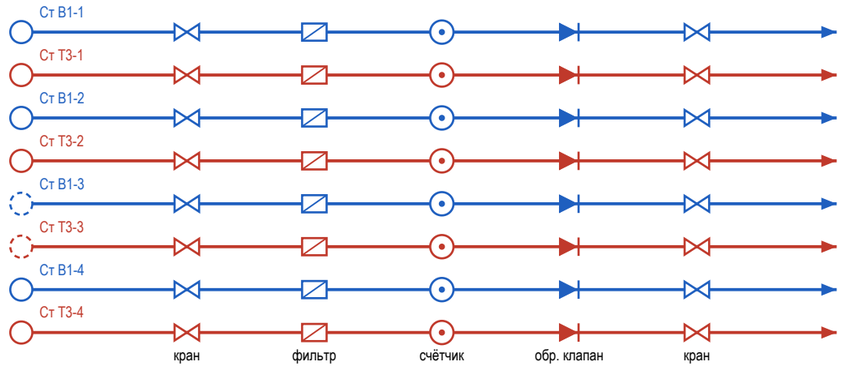

состав узла — по согласованию

⊗ Ст К1-1, Ст К1-2 (кухня), Ст К1-3, Ст К1-4 (постирочная): ревизия на стояке — люк в коробе


Примечания

1. Трассы принципиальные, построены от стояков вдоль стен помещений; фактическое положение фиксируется исполнительной схемой с привязками (фото с рулеткой) до закрытия.
2. Уклон К1 не менее 1/d и не более 150 мм/м (СП 30.13330.2020, п. 19.1), приняты практические уклоны; поворот — двумя отводами 45°, ревизия после поворота, доступ сохранить. Стояк К1 в коробе — звукоизоляция стояка в коробе, без жёсткого контакта короба с трубой.
3. Решение по К1: стяжка 35 мм не укрывает трубы (нужно Ø + Δh + 45 мм) — выпуски идут над чистым полом вдоль стен: К1-8, К1-9 — за приборами и в раме инсталляции; К1-6, К1-1, К1-7, К1-3, К1-4, К1-5 — в коробе ГКЛВ под плитку (размеры в профиле). Короба — на развёртках; отметку низа врезки в стояк замерить до черновых работ.
4. К1-2 (С_02 унитаз подвесной): трасса К1 до Ст К1-1 — под проёмом Д-5, короб там не поставить: прибор ближе к стояку, выпуск в полу с подъёмом пола или насосная установка (КНС) — решение заказчика; до решения не выполнять.
5. Состав узла ввода В1, Т3 — по согласованию: на схеме типовой узел — кран шаровой, фильтр, счётчик, обратный клапан, кран; состав и места не определены (записи реестра нет). Доступ к арматуре — через люк не меньше 300×400. Водопровод — в штробе стен или в коробах; трубы испытать давлением до закрытия (акт скрытых работ).
6. Расчёт систем, диаметры магистралей и подбор оборудования выполняет проектная организация; врезка и перенос стояков — по согласованию с управляющей организацией. Арматуру и привязки сверить по паспортам приборов.
7. Ст К1-3, Ст В1-3, Ст Т3-3 на обмере не показаны: положение принято, не замерено; положение сверить на объекте до разводки.

					Проект: Квартира 103 м²
	Лист	№ док.	Подпись	Дата	Схема разводки водопровода и канализации
Дизайнер	Кырлан А.С.			04.11.26	

Стадия	Лист	Листов
П	19	96

Схема В1 (М 1:50; по вертикали и горизонтали один масштаб, глубина — ×0,5 под 45°)

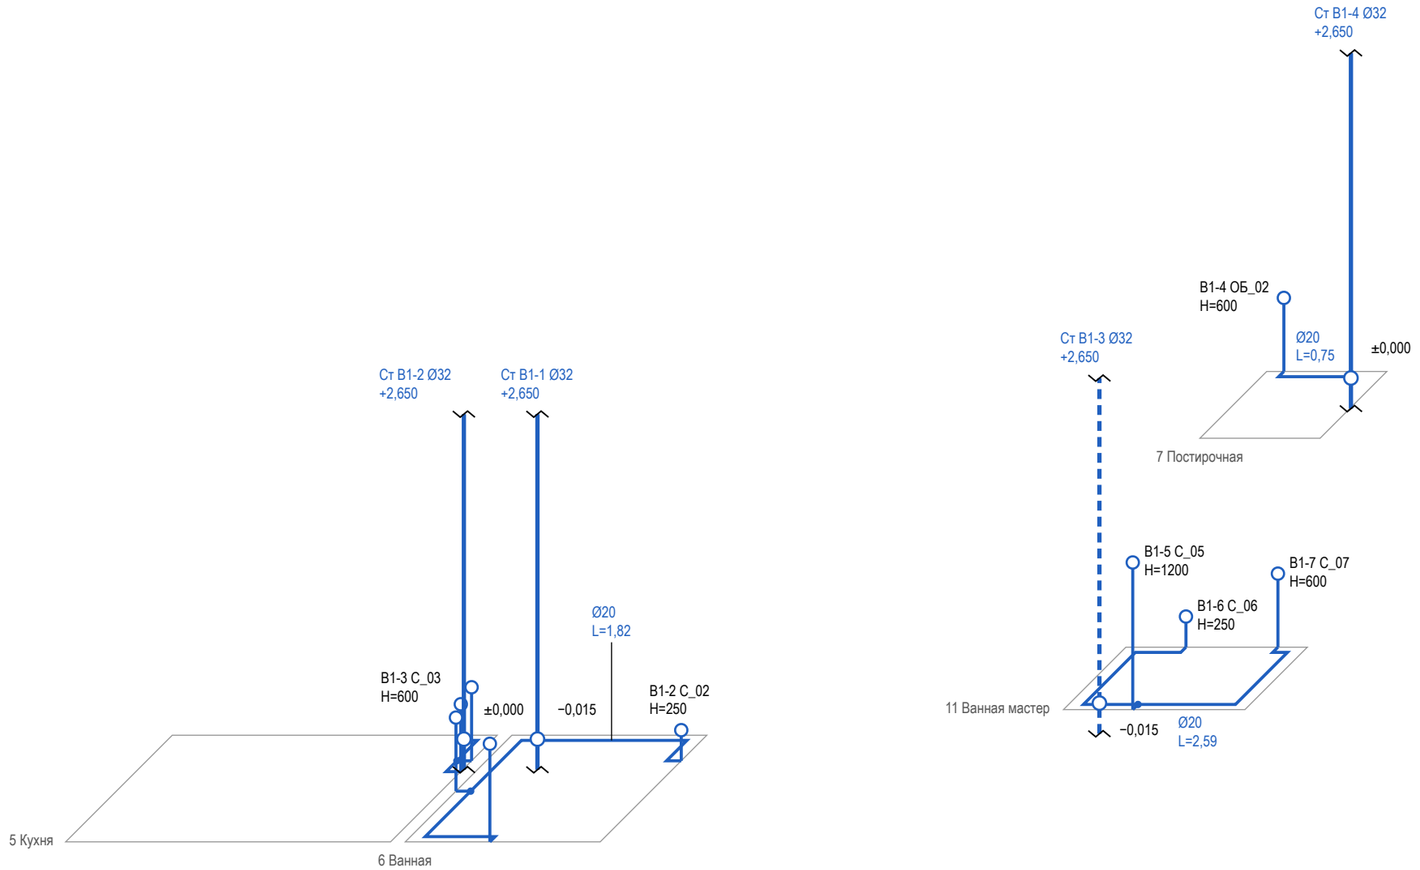

Условные обозначения


- В1 — водопровод хозяйственно-питьевой (ХВС), PP-R Ø20
- вывод В1 (код — в ведомости привязок)
- стояк «Ст К1-N / Ст В1-N» (ГОСТ 21.601), Ø мм
- стояк в плане (на отметке пола); вертикаль — стояк по высоте, разрыв — перекрытие
- тройник (ответвление к прибору)
- кран шаровой
- стояк Т3 не на обмере — принят в шахте рядом со Ст В1, сверить

Примечания

1. Схема В1 построена по тем же трассам, что план разводки: положение в плане сохранено, глубина — в масштабе ×0,5. Трассы принципиальные; фактическое положение фиксируется исполнительной схемой до закрытия.
2. Высоты Н — от чистого пола помещения, мм. Отметка прокладки магистрали В1 (в стяжке, в стене или по полу) в данных не задана: участки показаны на уровне пола условно (записи реестра нет).
3. Узел ввода В1 (кран, фильтр, счётчик, обратный клапан, кран) — на схеме разводки; состав узла ввода — по согласованию. Кран шаровой — на первом участке от стояка.
4. Ст В1-3 на обмере не показаны: положение принято, не замерено; положение сверить на объекте до разводки.
5. Трубы испытать давлением до закрытия (акт скрытых работ, опрессовка по СП 73.13330.2016).
6. Диаметры, высоты выводов и места кранов — по паспортам выбранных приборов и расчёту проектной организации.
7. Расчёт систем, диаметры магистралей и подбор оборудования выполняет проектная организация.

					Проект: Квартира 103 м²	М 1:50
	Лист	№ док.	Подпись	Дата		
Дизайнер	Кырлан А.С.			04.11.26	Аксонометрическая схема В1 (холодное водоснабжение)	Стадия: П; Лист: 20; Листов: 96

Схема Т3 (М 1:100; по вертикали и горизонтали один масштаб, глубина — ×0,5 под 45°)

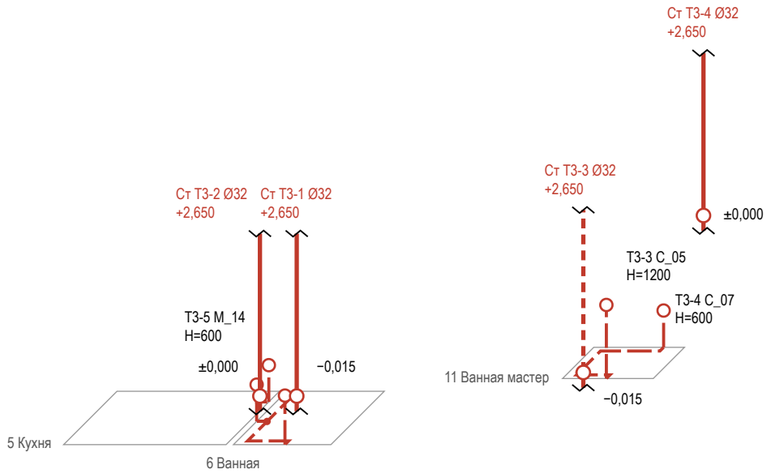

Условные обозначения


- Т3 — горячее водоснабжение, подача (ГВС), PP-R Ø20
- вывод Т3 (код — в ведомости привязок)
- стояк «Ст К1-N / Ст В1-N» (ГОСТ 21.601), Ø мм
- стояк в плане (на отметке пола); вертикаль — стояк по высоте, разрыв — перекрытие
- тройник (ответвление к прибору)
- кран шаровой
- стояк Т3 не на обмере — принят в шахте рядом со Ст В1, сверить

Примечания

1. Схема Т3 построена по тем же трассам, что план разводки: положение в плане сохранено, глубина — в масштабе ×0,5. Трассы принципиальные; фактическое положение фиксируется исполнительной схемой до закрытия.
2. Высоты Н — от чистого пола помещения, мм. Отметка прокладки магистрали Т3 (в стяжке, в стене или по полу) в данных не задана: участки показаны на уровне пола условно (записи реестра нет).
3. Узел ввода Т3 (кран, фильтр, счётчик, обратный клапан, кран) — на схеме разводки; состав узла ввода — по согласованию. Кран шаровой — на первом участке от стояка.
4. Циркуляция ГВС в данных не задана — циркуляционного трубопровода на схеме нет (записи реестра нет).
5. Ст Т3-3 на обмере не показаны: положение принято, не замерено; положение сверить на объекте до разводки.
6. Трубы испытать давлением до закрытия (акт скрытых работ, опрессовка по СП 73.13330.2016).
7. Диаметры, высоты выводов и места кранов — по паспортам выбранных приборов и расчёту проектной организации.
8. Расчёт систем, диаметры магистралей и подбор оборудования выполняет проектная организация.

					Проект: Квартира 103 м²	М 1:100
	Лист	№ док.	Подпись	Дата		
Дизайнер	Кырлан А.С.			04.11.26	Аксонометрическая схема Т3 (горячее водоснабжение)	Стадия: П; Лист: 21; Листов: 96

Схема К1 (М 1:50; по вертикали и горизонтали один масштаб, глубина — ×0,5 под 45°)

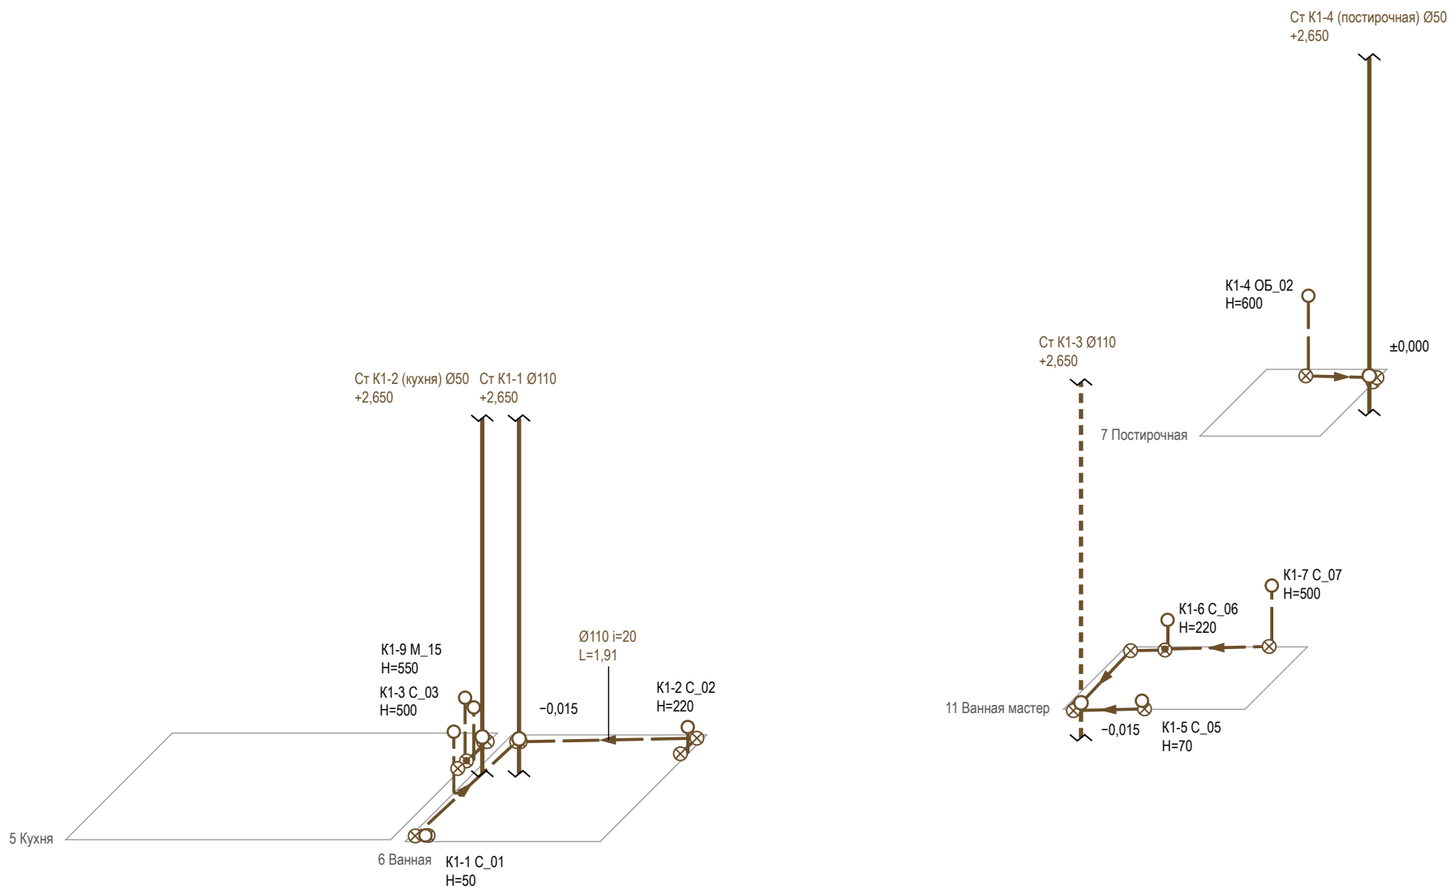

Условные обозначения


- К1 — канализация бытовая
- вывод К1 (код — в ведомости привязок)
- стояк «Ст К1-N / Ст В1-N» (ГОСТ 21.601), Ø мм
- стояк в плане (на отметке пола); вертикаль — стояк по высоте, разрыв — перекрытие
- направление уклона К1 / пола: Ø, мм на 1 м
- ревизия (прочистка) К1 — доступ сохранить
- тройник (ответвление к прибору)
- стояк Т3 не на обмере — принят в шахте рядом со Ст В1, сверить

Примечания

1. Схема К1 построена по тем же трассам, что план разводки: положение в плане сохранено, глубина — в масштабе ×0,5. Трассы принципиальные; фактическое положение фиксируется исполнительной схемой до закрытия.
2. Отметки — от плиты перекрытия: низ трубы у врезки в стояк — отметка из данных выпуска, к прибору труба поднимается на уклон i, мм/м (уклон не менее 1/d и не более 150 мм/м, СП 30.13330.2020, п. 19.1); чистый пол — выше плиты на стяжку (высота пирога пола). Высота выпуска прибора Н — от чистого пола.
3. Ревизия — на повороте и в начале участка; стояк К1 в коробе с люком — звукоизоляция стояка в коробе; поворот — двумя отводами 45°.
4. Ст К1-3 на обмере не показаны: положение принято, не замерено; положение сверить на объекте до разводки.
5. Трубы испытать давлением до закрытия (акт скрытых работ, опрессовка по СП 73.13330.2016).
6. Диаметры, высоты выводов и места кранов — по паспортам выбранных приборов и расчёту проектной организации.
7. Расчёт систем, диаметры магистралей и подбор оборудования выполняет проектная организация.

					Проект: Квартира 103 м²	М 1:50
	Лист	№ док.	Подпись	Дата		
Дизайнер	Кырлан А.С.			04.11.26	Аксонометрическая схема К1 (канализация)	Стадия: П; Лист: 22; Листов: 96

Стена Б (М 1:20)

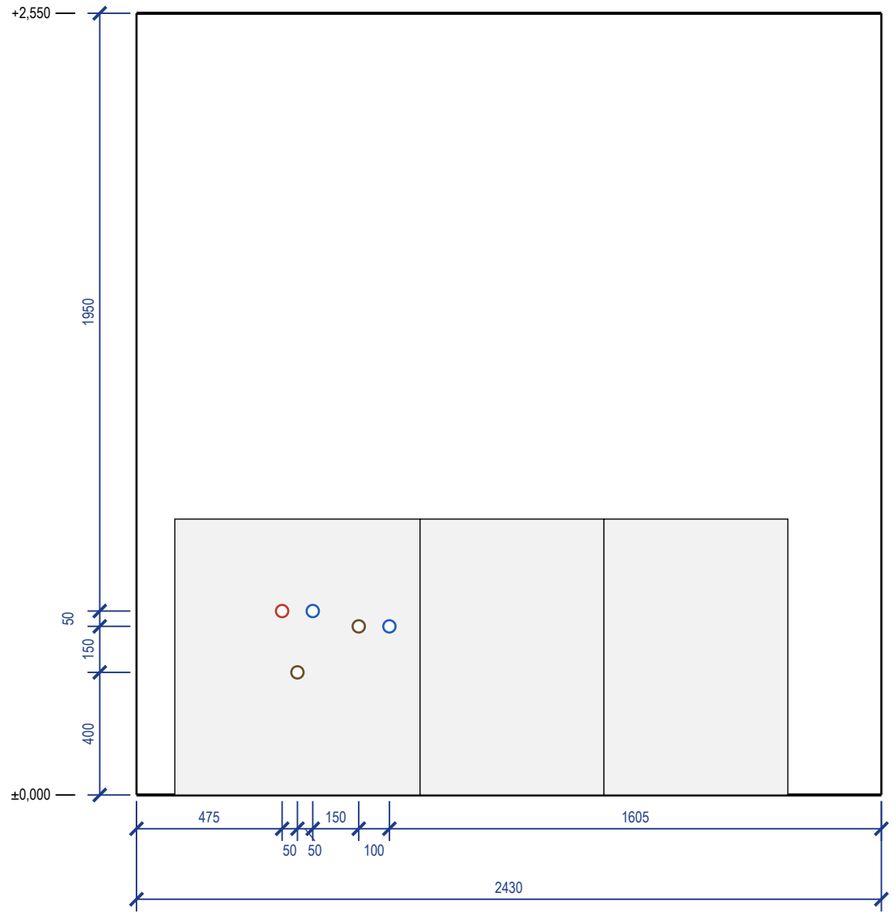

Ведомость привязок выводов (от чистого пола и угла)

Код	Прибор	Ø	H, мм	Привязка, мм
В1-8	М_14 мойка кухонная	½"	600	ст. Б: 575 от лев. угла
Т3-5	М_14 мойка кухонная	½"	600	ст. Б: 475 от лев. угла
К1-8	М_14 мойка кухонная	Ø50	400	ст. Б: 525 от лев. угла
В1-9	М_15 посудомоечная машина	½"	550	ст. Б: 825 от лев. угла
К1-9	М_15 посудомоечная машина	Ø40	550	ст. Б: 725 от лев. угла

Условные обозначения


- вывод В1 (код — в ведомости привязок)
- вывод Т3 (код — в ведомости привязок)
- вывод К1 (код — в ведомости привязок)
- сантехприбор по расстановке (габарит модели)
- дверной проём; окно — сплошной контур

Примечания


1. Габариты и высоты приборов, межосевые смесителей и места кранов — по паспортам выбранных приборов, сверяются до разметки стен.
2. Высоты H — от чистого пола помещения, мм; отметка чистого пола и потолка — у левого края вида (от ±0,000 объекта). Привязки — от левого чистового угла вида (облицовка стен вычтена), как на развёртках стен.
3. Стояки в помещении: Ст К1-2 (кухня) Ø50, Ст В1-2 Ø32, Ст Т3-2 Ø32 — положение на плане выводов; выводы подключаются к ним по схеме разводки.
4. Ревизионные люки к арматуре и ревизиям в данных не заданы: место и размер не определены (записи реестра нет).
5. Мойка, ПММ и фильтр — выводы в шкафу мойки; диаметры и положение сифона и кранов сверить по паспортам приборов и чертежам модуля.
6. Часть подписей выводов не уместилась у знака: коды и высоты — в ведомости привязок.
7. Расчёт систем водоснабжения и канализации и подбор оборудования выполняет проектная организация; лист задаёт места и высоты выводов.

					Проект: Квартира 103 м²	М 1:20
	Лист	№ док.	Подпись	Дата		
Дизайнер	Кырлан А.С.			04.11.26	Развёртки мокрых зон: выводы ВК. Кухня	Стадия: П; Лист: 23; Листов: 96


Стена Б (М 1:25)

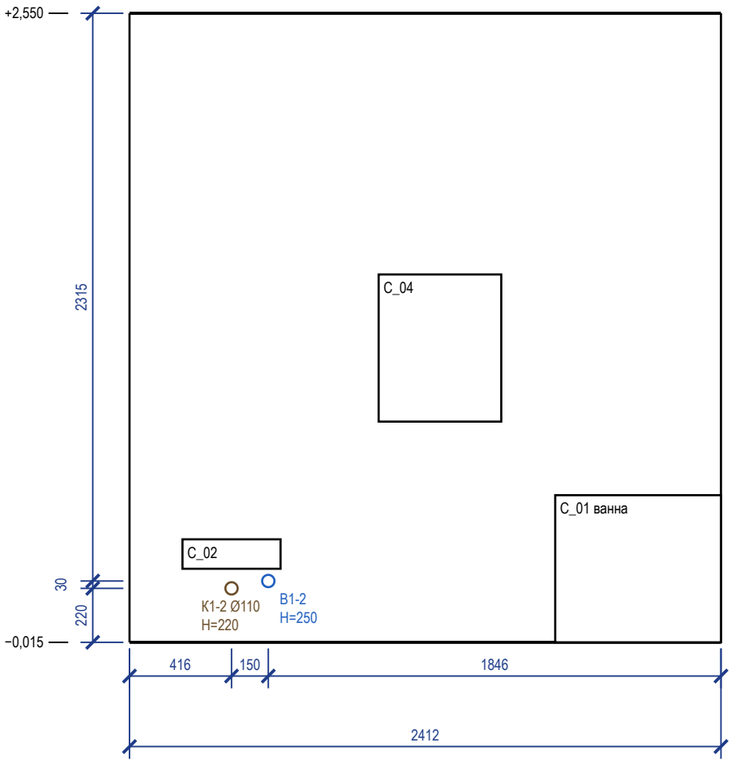

Стена В (М 1:25)

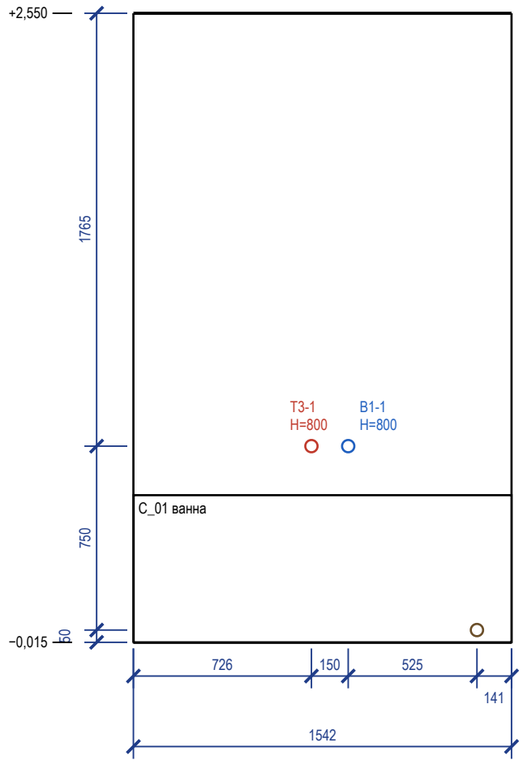

Стена Г (М 1:25)

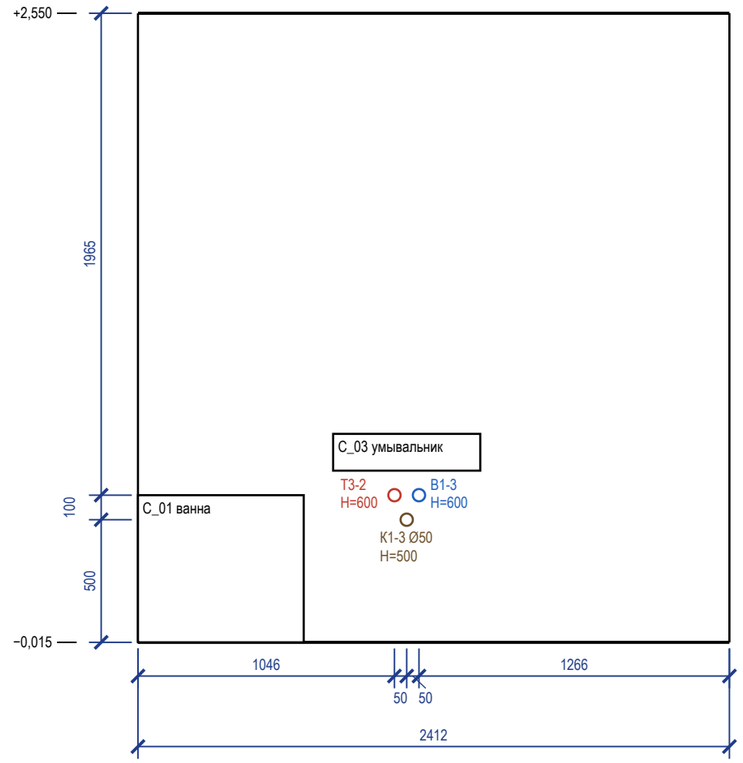

Ведомость привязок выводов (от чистого пола и угла)

Код	Прибор	Ø	H, мм	Привязка, мм
B1-2	C_02 унитаз подвесной	½"	250	ст. Б: 566 от лев. угла
K1-2	C_02 унитаз подвесной	Ø110	220	ст. Б: 416 от лев. угла
B1-1	C_01 ванна	½"	800	ст. В: 876 от лев. угла
T3-1	C_01 ванна	½"	800	ст. В: 726 от лев. угла
K1-1	C_01 ванна	Ø50	50	ст. В: 1401 от лев. угла
B1-3	C_03 умывальник	½"	600	ст. Г: 1146 от лев. угла
T3-2	C_03 умывальник	½"	600	ст. Г: 1046 от лев. угла
K1-3	C_03 умывальник	Ø50	500	ст. Г: 1096 от лев. угла

Условные обозначения


- вывод B1 (код — в ведомости привязок)
- вывод T3 (код — в ведомости привязок)
- вывод K1 (код — в ведомости привязок)
- сантехприбор по расстановке (габарит модели)
- дверной проём; окно — сплошной контур

Примечания


1. Габариты и высоты приборов, межосевые смесителей и места кранов — по паспортам выбранных приборов, сверяются до разметки стен.
2. Высоты H — от чистого пола помещения, мм; отметка чистого пола и потолка — у левого края вида (от ±0,000 объекта). Привязки — от левого чистового угла вида (облицовка стен вычтена), как на развёртках стен.
3. Стояки в помещении: Ст K1-1 Ø110, Ст B1-1 Ø32, Ст T3-1 Ø32 — положение на плане выводов; выводы подключаются к ним по схеме разводки.
4. Ревизионные люки к арматуре и ревизиям в данных не заданы: место и размер не определены (записи реестра нет).
5. Часть подписей выводов не уместилась у знака: коды и высоты — в ведомости привязок.
6. Расчёт систем водоснабжения и канализации и подбор оборудования выполняет проектная организация; лист задаёт места и высоты выводов.

					Проект: Квартира 103 м²	М 1:25
	Лист	№ док.	Подпись	Дата		
Дизайнер	Кырлан А.С.			04.11.26	Развёртки мокрых зон: выводы ВК. Ванная	Стадия: П; Лист: 24; Листов: 96

Стена А (М 1:20)

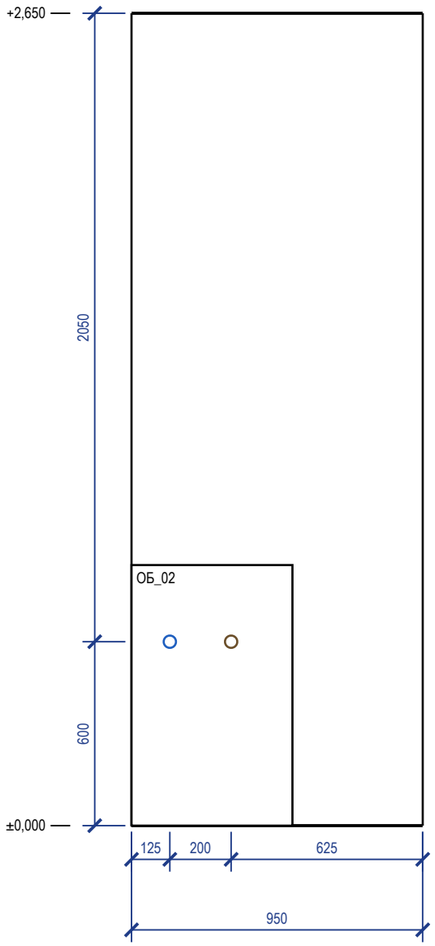

Стена Г (М 1:20)

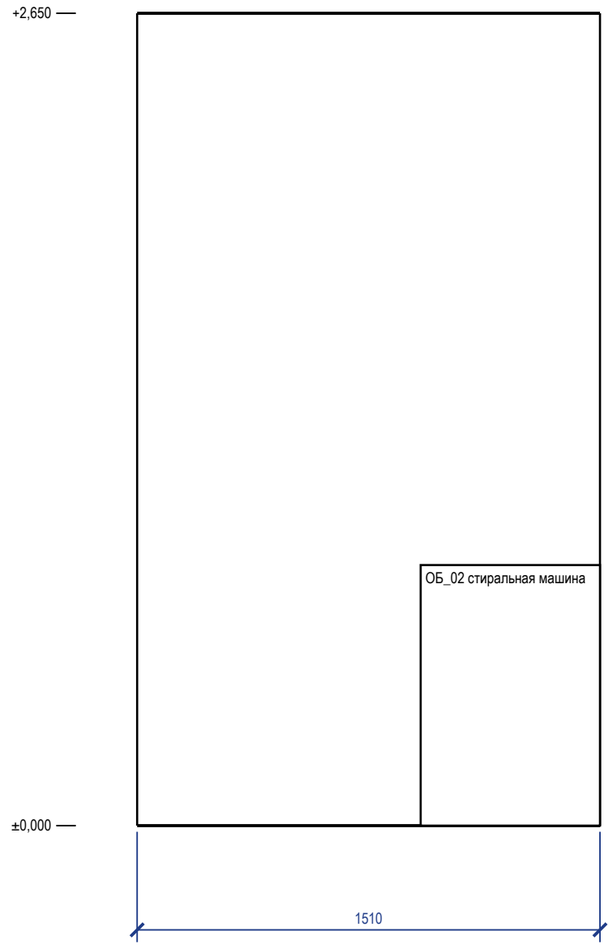

Ведомость привязок выводов (от чистого пола и угла)

Код	Прибор	Ø	H, мм	Привязка, мм
В1-4	ОБ_02 стиральная машина	½"	600	ст. А: 125 от лев. угла
К1-4	ОБ_02 стиральная машина	Ø50	600	ст. А: 325 от лев. угла

Условные обозначения


- вывод В1 (код — в ведомости привязок)
- вывод Т3 (код — в ведомости привязок)
- вывод К1 (код — в ведомости привязок)
- сантехприбор по расстановке (габарит модели)
- дверной проём; окно — сплошной контур

Примечания


1. Габариты и высоты приборов, межосевые смесителей и места кранов — по паспортам выбранных приборов, сверяются до разметки стен.
2. Высоты H — от чистого пола помещения, мм; отметка чистого пола и потолка — у левого края вида (от ±0,000 объекта). Привязки — от левого чистового угла вида (облицовка стен вычтена), как на развёртках стен.
3. Стояки в помещении: Ст К1-4 (постирочная) Ø50, Ст В1-4 Ø32, Ст Т3-4 Ø32 — положение на плане выводов; выводы подключаются к ним по схеме разводки.
4. Ревизионные люки к арматуре и ревизиям в данных не заданы: место и размер не определены (записи реестра нет).
5. Часть подписей выводов не уместилась у знака: коды и высоты — в ведомости привязок.
6. Расчёт систем водоснабжения и канализации и подбор оборудования выполняет проектная организация; лист задаёт места и высоты выводов.

					Проект: Квартира 103 м²	М 1:20
	Лист	№ док.	Подпись	Дата		
Дизайнер	Кырлан А.С.			04.11.26	Развёртки мокрых зон: выводы ВК. Постирочная	Стадия: П; Лист: 25; Листов: 96


Стена А (М 1:20)

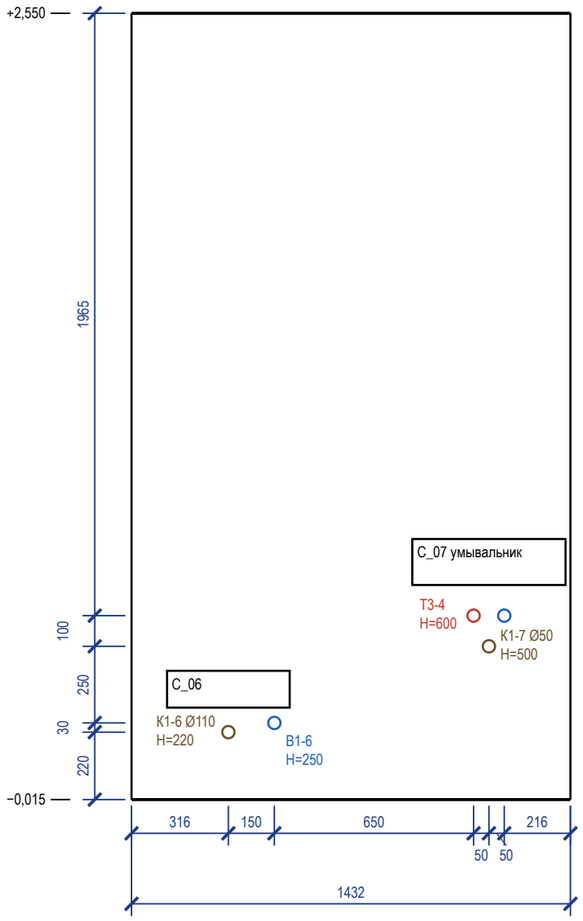

Стена Б (М 1:20)

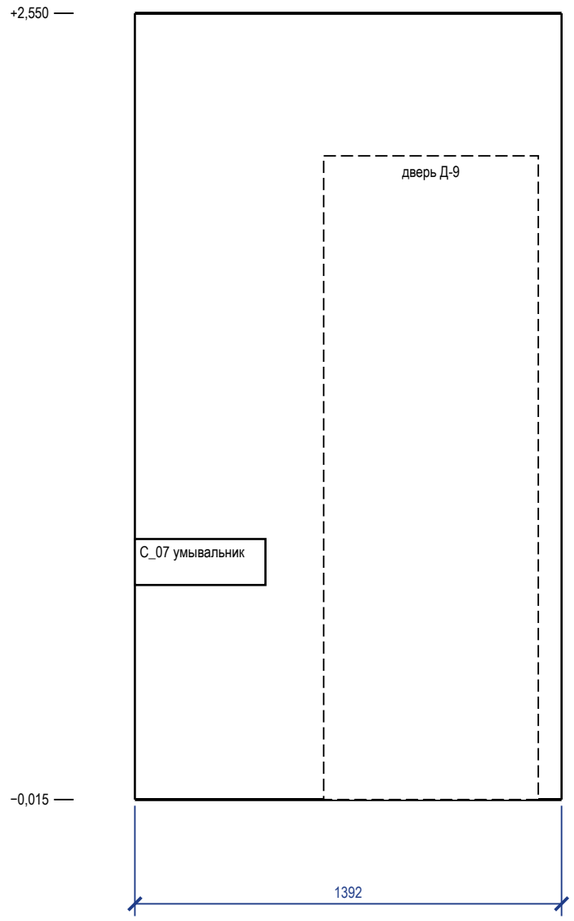

Стена В (М 1:20)

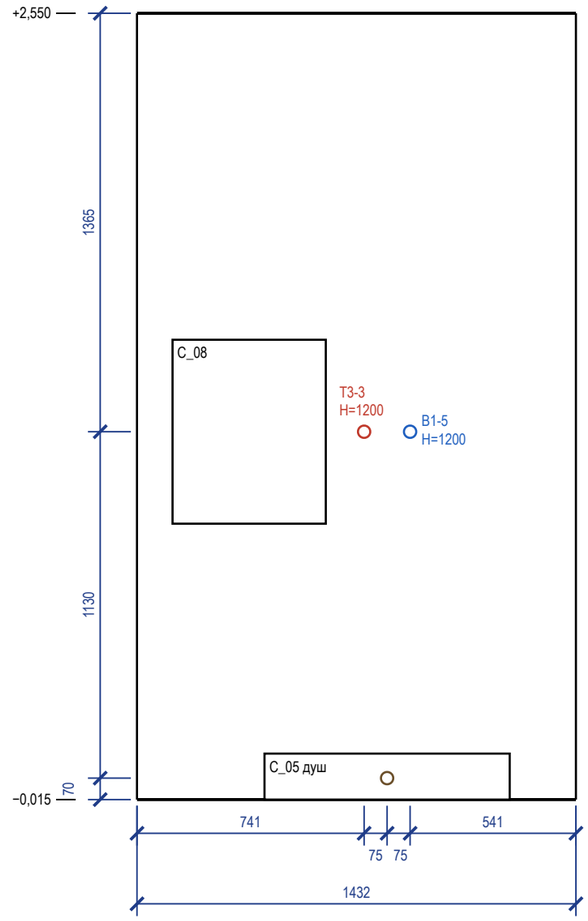

Ведомость привязок выводов (от чистого пола и угла)

Код	Прибор	Ø	H, мм	Привязка, мм
B1-6	C_06 унитаз подвесной	½"	250	ст. А: 466 от лев. угла
K1-6	C_06 унитаз подвесной	Ø110	220	ст. А: 316 от лев. угла
B1-7	C_07 умывальник	½"	600	ст. А: 1216 от лев. угла
T3-4	C_07 умывальник	½"	600	ст. А: 1116 от лев. угла

Ведомость привязок (продолжение)

Код	Прибор	Ø	H, мм	Привязка, мм
K1-7	C_07 умывальник	Ø50	500	ст. А: 1166 от лев. угла
B1-5	C_05 душ	½"	1200	ст. В: 891 от лев. угла
T3-3	C_05 душ	½"	1200	ст. В: 741 от лев. угла
K1-5	C_05 душ	Ø50	70	ст. В: 816 от лев. угла

Условные обозначения

- вывод B1 (код — в ведомости привязок)
- вывод T3 (код — в ведомости привязок)
- вывод K1 (код — в ведомости привязок)
- сантехприбор по расстановке (габарит модели)
- дверной проём; окно — сплошной контур

Примечания

1. Габариты и высоты приборов, межосевые смесителей и места кранов — по паспортам выбранных приборов, сверяются до разметки стен.
2. Высоты H — от чистого пола помещения, мм; отметка чистого пола и потолка — у левого края вида (от ±0,000 объекта). Привязки — от левого чистового угла вида (облицовка стен вычтена), как на развёртках стен.
3. Стояки в помещении: Ст K1-3 Ø110, Ст B1-3 Ø32, Ст T3-3 Ø32 — положение на плане выводов; выводы подключаются к ним по схеме разводки.
4. Ревизионные люки к арматуре и ревизиям в данных не заданы: место и размер не определены (записи реестра нет).
5. Часть подписей выводов не уместилась у знака: коды и высоты — в ведомости привязок.
6. Расчёт систем водоснабжения и канализации и подбор оборудования выполняет проектная организация; лист задаёт места и высоты выводов.

	Лист	№ док.	Подпись	Дата
Дизайнер	Кырлан А.С.			04.11.26

Проект: Квартира 103 м² — **М 1:20**

Развёртки мокрых зон: выводы ВК. Ванная мастер

Стадия	Лист	Листов
П	26	96


выпуск 04.11.2026 № d6a6e5e88d · стр. 26 из 96

Поз.	Наименование и техническая характеристика	Тип, марка, обозначение документа	Код продукции	Поставщик	Ед. изм.	Кол.	Масса 1 ед., кг	Примечание
	Санитарные приборы							
1	Ванна встраиваемая акриловая 1600×700 мм, с каркасом, экраном и отверстием слив-перелив	аналог		выбор заказчика	шт	1		С_01
2	Унитаз подвесной безободковый, с сиденьем микролифт, крепёж и звукоизолирующая прокладка	Jacob Delafon Struktura EDF102-00		выбор заказчика	шт	2		С_02, С_06
3	Инсталляция для подвесного унитаза: рама высотой 1120 мм, бачок, клавиша смыва (ось клавиши 1050 мм от чистого пола)	аналог		выбор заказчика	шт	2		С_02, С_06; короб ГКЛВ
4	Умывальник подвесной 600×450 мм, с отверстием под смеситель и переливом	аналог		выбор заказчика	шт	1		С_03
5	Умывальник подвесной 500×450 мм, с отверстием под смеситель и переливом	аналог		выбор заказчика	шт	1		С_07
6	Поддон душевой низкий 800×800 мм, с сифоном и выпуском Ø50, на ножках/подиуме	аналог		выбор заказчика	шт	1		С_05
7	Мойка кухонная врезная / подстольная, с переливом, ориентир 700×480 мм — в модуле М_14 шириной 800 мм, вырез по шаблону модели	аналог		с кухонной мебелью	шт	1		М_14
8	Полотенцесушитель электрический, IP44, с терморегулятором	аналог		выбор заказчика	шт	2		С_04, С_08
	Смесители, сифоны и арматура приборов							
9	Смеситель для ванны настенный однорычажный, межосевое 150 мм, с душевым набором (лейка, шланг, держатель)	аналог		выбор заказчика	шт	1		С_01
10	Смеситель для умывальника однорычажный, с донным клапаном	аналог		выбор заказчика	шт	2		С_03, С_07
11	Душевая система скрытого монтажа с термостатом: встраиваемая часть, верхний душ, ручная лейка	аналог		выбор заказчика	шт	1		С_05; встраиваемая часть — до плитки
12	Смеситель кухонный однорычажный, высокий излив	аналог		выбор заказчика	шт	1		М_14
13	Обвязка ванны слив-перелив Ø40/50 с сифоном	аналог		выбор заказчика	шт	1		С_01
14	Сифон для умывальника бутылочный Ø32/40–50, с гофрой к выпуску	аналог		выбор заказчика	шт	2		С_03, С_07
15	Сифон для мойки Ø40/50	аналог		выбор заказчика	шт	1		М_14
16	Сифон для посудомоечной машины с обратным клапаном, на выводе слива Ø40	аналог		выбор заказчика	шт	1		М_15
17	Сифон для стиральной машины встраиваемый в стену Ø50, с обратным клапаном	аналог		выбор заказчика	шт	1		ОБ_02
18	Кран угловой ½"×½" с гибкой подводкой 40 см (умывальники, мойка)	аналог		выбор заказчика	шт	6		по 2 на прибор
19	Кран шаровой угловой ½"×¾" для подключения стиральной и посудомоечной машины	аналог		выбор заказчика	шт	2		ОБ_02, М_15
	Трубопроводы							
20	Труба полипропиленовая PP-R PN20 Ø20×3,4 (В1)	ГОСТ 32415-2013		выбор заказчика	м	19	0,17	11,4 + 5,5 + 10 %
21	Труба PP-R, армированная стекловолокном, PN20 Ø20×2,8 (Т3)	ГОСТ 32415-2013		выбор заказчика	м	12	0,15	6,9 + 3,8 + 10 %
22	Труба канализационная ПП Ø40 (К1)	ГОСТ 32414-2013		выбор заказчика	м	1		0,3 + 0,6 + 10 %
23	Труба канализационная ПП Ø50 (К1)	ГОСТ 32414-2013		выбор заказчика	м	8,5		5,6 + 2,1 + 10 %
24	Труба канализационная ПП Ø110 (К1)	ГОСТ 32414-2013		выбор заказчика	м	4,5		3,5 + 0,4 + 10 %
	Фасонные части и выводы							
25	Отвод канализационный ПП 45° Ø40	ГОСТ 32414-2013		выбор заказчика	шт	2		2 шт. на поворот
26	Отвод канализационный ПП 45° Ø50	ГОСТ 32414-2013		выбор заказчика	шт	24		2 шт. на поворот
27	Отвод канализационный ПП 45° Ø110	ГОСТ 32414-2013		выбор заказчика	шт	12		2 шт. на поворот
28	Тройник канализационный ПП 45° (врезки ветвей)	ГОСТ 32414-2013		выбор заказчика	шт	8		
29	Ревизия канализационная ПП (после поворота трассы)	ГОСТ 32414-2013		выбор заказчика	шт	11		доступ сохранить
30	Фитинги PP-R Ø20: тройники, угольники 90° (ветви и повороты В1, Т3)	ГОСТ 32415-2013		выбор заказчика	шт	42		
31	Водорозетка PP-R Ø20×½" настенная, с креплением	ГОСТ 32415-2013		выбор заказчика	шт	14		коды — лист выводов
	Узлы ввода, люки, короба							
32	Кран шаровой латунный Ду15 PN16 (отключение ввода)	аналог		выбор заказчика	шт	8		Ст В1-1, Ст Т3-1, Ст В1-2, Ст Т3-2, Ст В1-3, Ст Т3-3, Ст В1-4, Ст Т3-4
33	Фильтр сетчатый косой Ду15	аналог		выбор заказчика	шт	8		
34	Счётчик воды крыльчатый Ду15 (ХВ, ГВ), с поверкой	аналог		выбор заказчика	шт	8		пломба УК
35	Клапан обратный Ду15	аналог		выбор заказчика	шт	8		
36	Люк ревизионный нажимной под плитку 300×400 мм	аналог		выбор заказчика	шт	4		к стоякам и арматуре
37	Звукоизоляция стояка К1 в коробе: рулонный звукоизоляционный материал ≥ 10 мм, обмотка стояка на высоту этажа	аналог		выбор заказчика	м	10,8		Ст К1-1, Ст К1-2 (кухня), Ст К1-3, Ст К1-4 (постирочная)
38	Короб К1 над полом: профиль ПН/ПС, ГКЛВ 12,5 мм под плитку	аналог		выбор заказчика	м	7,8		сечение — лист разводки

Примечания

1. Форма 1 ГОСТ 21.110-2013, ширины граф изменены по п. 4.1. «Аналог» — аналог по характеристикам: модели внести до черновых работ, привязки выводов сверить по паспортам.
2. Бытовая техника не входит (показана арматура подключения), мойка — в комплекте кухни (марка — модуля кухни, как у столяра). Длины труб — трасса листа разводки + подъёмы + 10 %.
3. Стояк К1 в коробе — звукоизоляция стояка в коробе без жёсткого контакта короба с трубой.
4. Расчёт систем водоснабжения и канализации, диаметры магистралей и подбор оборудования выполняет проектная организация.

					Проект: Квартира 103 м²			
	Лист	№ док.	Подпись	Дата	Спецификация сантехнического оборудования	Стадия	Лист	Листов
Дизайнер	Кырлан А.С.			04.11.26		П	27	96

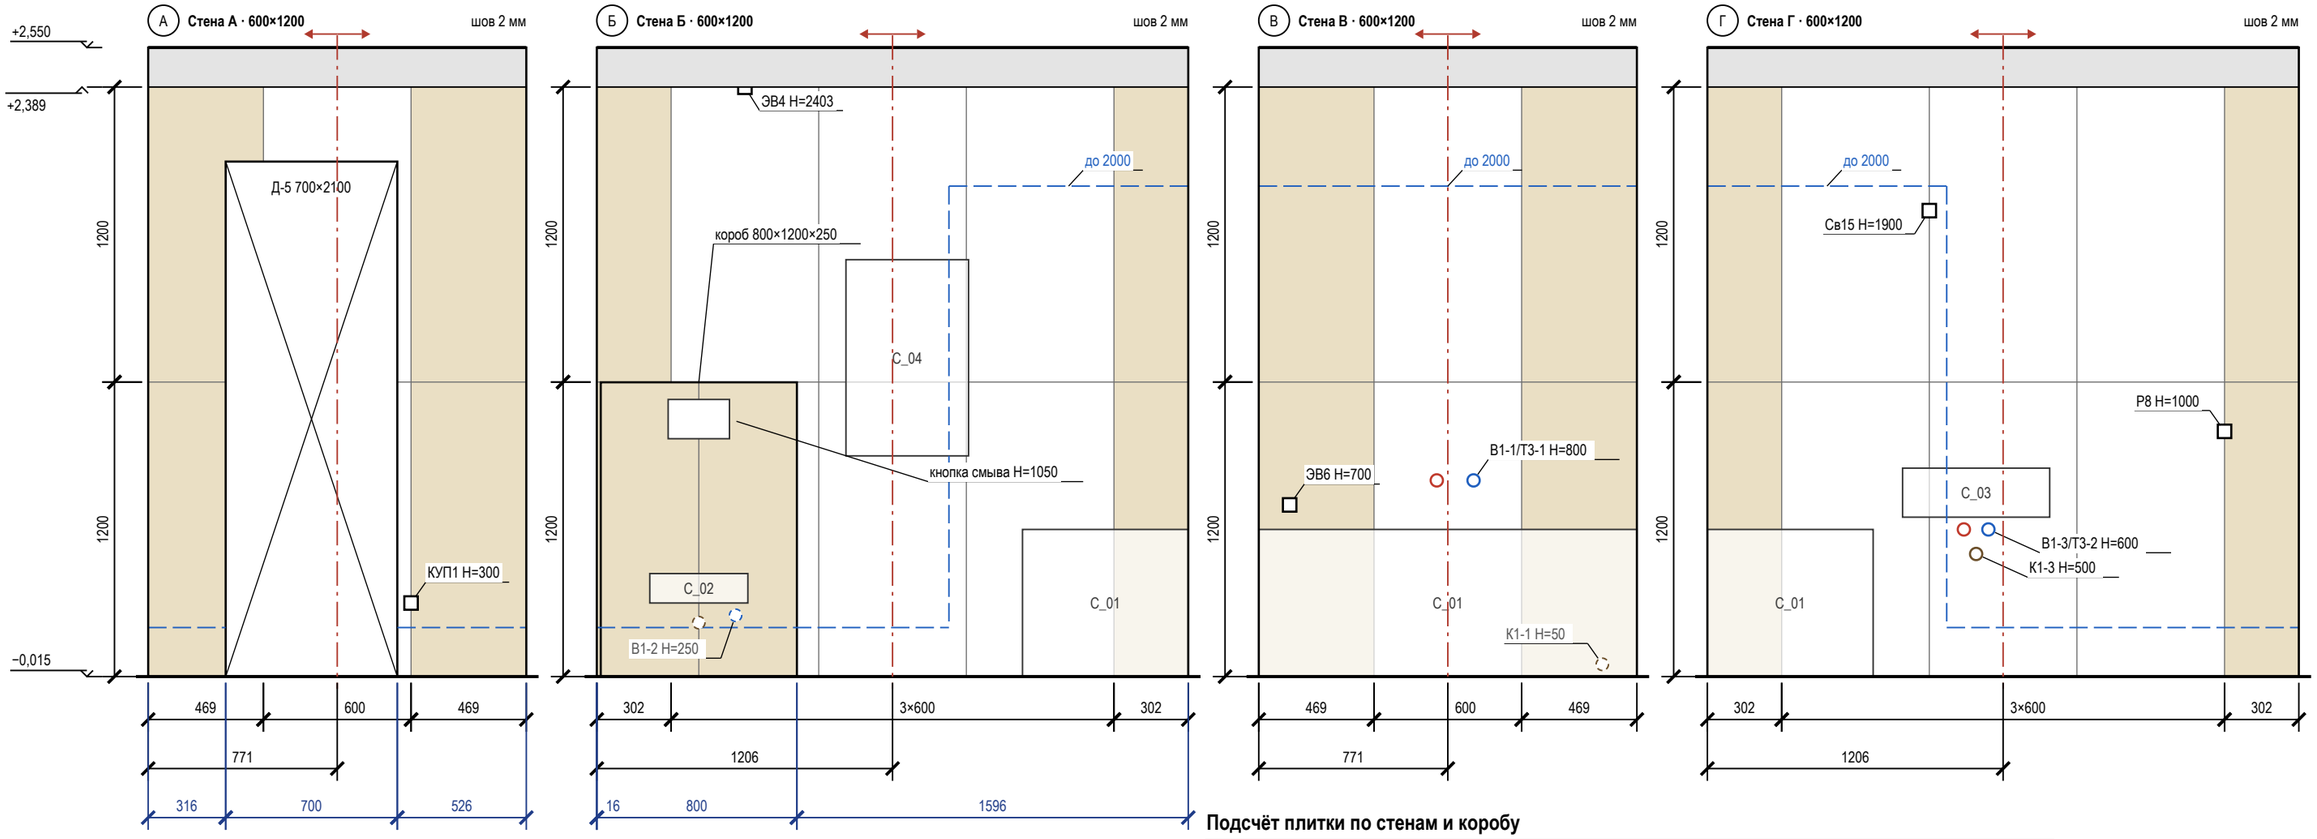

Условные обозначения

- плитка целая; тонкая линия — шов
- плитка с подрезкой (размер — на цепочке)
- ось старта; стрелки — направление укладки
- верх гидроизоляции: 200 от ЧП, в мокрой зоне — «до …»
- проём — не облицовывается
- сантехприбор: габарит, высота по практике
- короб инсталляции, в нём кнопка смыва 250×160
- вывод В1 (код — в ведомости привязок)
- вывод Т3 (код — в ведомости привязок)
- вывод К1 (код — в ведомости привязок)
- вывод за прибором / в коробе (не на сетке)
- электроточка: марка и H — по листам ЭОМ
- отметка уровня, м: ±0,000 — чистый пол жилых помещений
- низ потолка; серая полоса — стена без плитки
- А обозначение стены А–Г (как на развёртках)

Примечания

1. Вид изнутри, стены по часовой стрелке А → Г. Высоты — от чистого пола (−0,015), отметки — от ±0,000. Раскладка от чистовых размеров (штукатурка 10 + клей 5 + плитка 9 мм), подрезки чистые; старт — от оси стены, ряды от пола целыми.
2. Верх плитки +2,389, потолок +2,550, зазор 161 мм: потолок ГКЛ опустить до +2,392 (шов 3 мм, герметик) — согласовать с монтажником ГКЛ; иначе профиль-окантовка, полосу окрасить в цвет потолка. Подрезной ряд 156 мм не делать.
3. Точки из таблицы сдвигов переносятся до черновой разводки (ЭОМ — по тем же числам).
4. Выводы ВК стоят по оси прибора и с прибором не двигаются — привязки по «Плану выводов сантехники» без сдвига; вне сетки (В1-1/Т3-1, В1-3/Т3-2, К1-3) отверстие в плитке коронкой по той же привязке, плитку не сдвигать.
5. За приборами и в коробе (В1-2, К1-2, К1-1) — штриховым кольцом.
6. Гидроизоляция: 200 мм от ЧП по периметру; над ванной — до 2000 и 300 мм за борт (СП 29.13330.2011, п. 7.2 — на высоту замачивания); углы — лентой; акт скрытых работ, пролив.
7. Короб 800×1200×250: лицо 399 / 399 мм от оси кнопки смыва, боковины, полка; углы — запил 45° или профиль; за коробом плитку не кладут.
8. Между коробом и углом полоса 16 мм — довести короб до угла.


Подсчёт плитки по стенам и коробу


Поверхность	L × H, мм	S, м²	Целых	Подр.	С запасом	Подрезки: край / верх, мм
стена А	1542 × 2404	2,35	0	6	7	469 / 469; целый ряд
стена Б	2412 × 2404	4,95	5	5	11	302 / 302; целый ряд
короб (ст. Б)	800×1200×250	1,76	0	6	7	лицо 399 / 399; бок. 250
стена В	1542 × 2404	3,82	2	4	7	469 / 469; целый ряд
стена Г	2412 × 2404	5,91	6	4	11	302 / 302; целый ряд
Итого		**18,80**	**13**	**25**	**43**	


Сдвиг точек под раскладку

Точка (ВК, ЭОМ)	Стена	Проект: от угла / H	Под раскладку: от угла / H	Сдвиг, мм
ЭВ6	В	126 / 700	169 / 700	+43 в центр плитки

					Проект: Квартира 103 м²	**М 1:25**
	Лист	№ док.	Подпись	Дата	Раскладка плитки. Ванная. Развёртки стен	Стадия / Лист / Листов
Дизайнер	Кырлан А.С.			04.11.26		П / 28 / 96

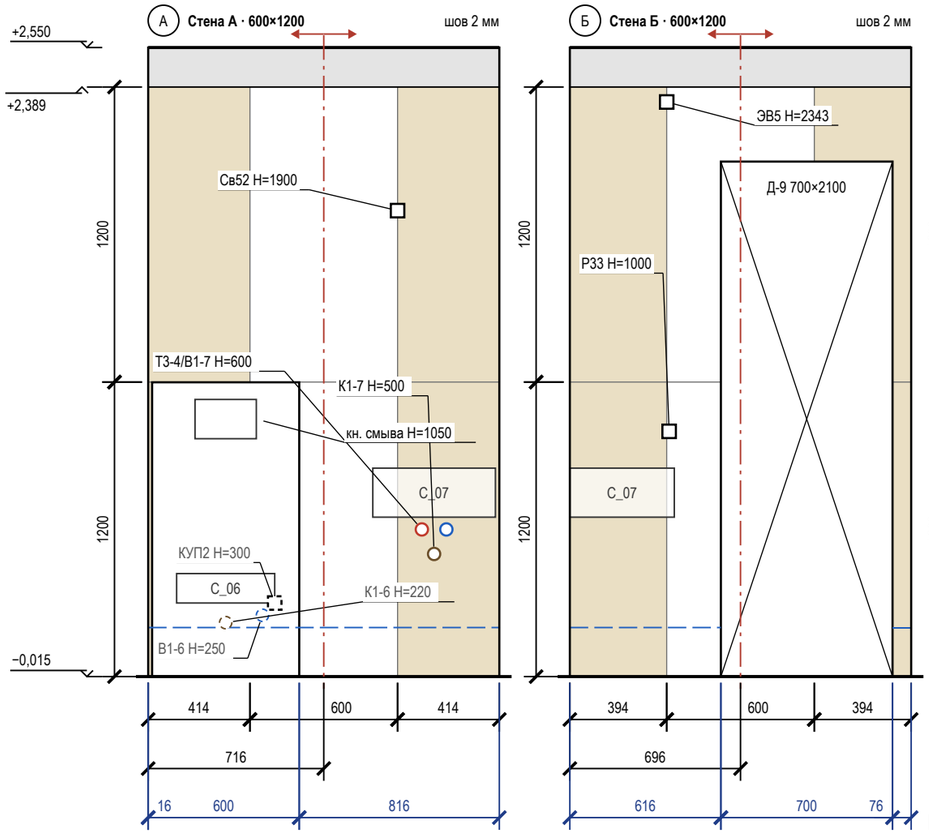

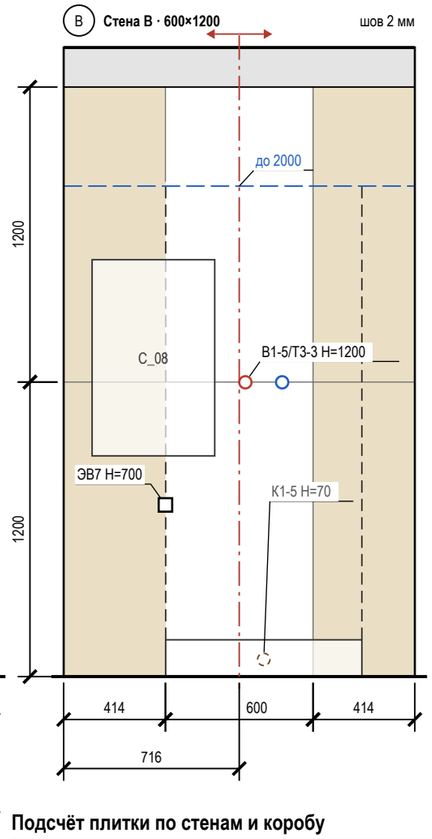

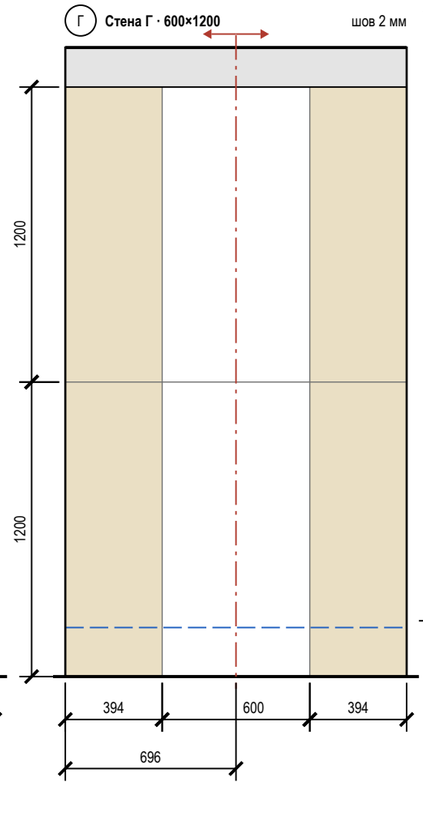

Условные обозначения

- плитка целая; тонкая линия — шов
- плитка с подрезкой (размер — на цепочке)
- ось старта; стрелки — направление укладки
- верх гидроизоляции: 200 от ЧП, в мокрой зоне — «до …»
- проём — не облицовывается
- сантехприбор: габарит, высота по практике
- граница душевой зоны (ограждение)
- короб инсталляции, в нём кнопка смыва 250×160
- вывод В1 (код — в ведомости привязок)
- вывод Т3 (код — в ведомости привязок)
- вывод К1 (код — в ведомости привязок)
- вывод за прибором / в коробе (не на сетке)
- электроточка: марка и Н — по листам ЭОМ
- отметка уровня, м: ±0,000 — чистый пол жилых помещений
- низ потолка; серая полоса — стена без плитки
- (А) обозначение стены А–Г (как на развёртках)

Подсчёт плитки по стенам и коробу

Поверхность	L × H, мм	S, м²	Целых	Подр.	С запасом	Подрезки: край / верх, мм
стена А	1432 × 2404	2,84	1	5	7	414 / 414; целый ряд
короб (ст. А)	600×1200×250	1,47	1	3	5	лицо 600; бок. 250
стена Б	1392 × 2404	1,99	0	6	7	394 / 394; целый ряд
стена В	1432 × 2404	3,56	2	4	7	414 / 414; целый ряд
стена Г	1392 × 2404	3,46	2	4	7	394 / 394; целый ряд
Итого		**13,32**	**6**	**22**	**33**	

Примечания

1. Вид изнутри, стены по часовой стрелке А → Г. Высоты — от чистого пола (−0,015), отметки — от ±0,000. Раскладка от чистовых размеров (штукатурка 10 + клей 5 + плитка 9 мм), подрезки чистые; старт — от оси стены, ряды от пола целыми.
2. Верх плитки +2,389, потолок +2,550, зазор 161 мм: потолок ГКЛ опустить до +2,392 (шов 3 мм, герметик) — согласовать с монтажником ГКЛ; иначе профиль-окантовка, полосу окрасить в цвет потолка. Подрезной ряд 156 мм не делать.
3. Открытые выводы и электроточки — на шве или в центре плитки (допуск 10 мм; плитка от 900 мм по высоте — на шве или не ближе 60 мм к нему).
4. Выводы ВК стоят по оси прибора и с прибором не двигаются — привязки по «Плану выводов сантехники» без сдвига; вне сетки (Т3-4/В1-7, К1-7, В1-5/Т3-3) — отверстие в плитке коронкой по той же привязке, плитку не сдвигать.
5. За приборами и в коробе (В1-6, К1-6, КУП2, К1-5) — штриховым кольцом.
6. Гидроизоляция: 200 мм от ЧП по периметру; у душа — до 2000 и 500 мм за поддон (СП 29.13330.2011, п. 7.2 — на высоту замачивания); углы — лентой; акт скрытых работ, пролив.
7. Короб 600×1200×250: лицо 600 мм от оси кнопки смыва, боковины, полка; углы — запил 45° или профиль; за коробом плитку не кладут.
8. Между коробом и углом полоса 16 мм — довести короб до угла.
9. Линии узора (швы плитки, складки штор, рёбра радиаторов) прерываются у знаков и выносок — просвет между линиями не менее 0,7 мм.

	Лист	№ док.	Подпись	Дата
Дизайнер	Кырлан А.С.			04.11.26


Проект: Квартира 103 м²

М 1:25

Раскладка плитки. Ванная мастер. Развёртки стен

Стадия	Лист	Листов
П	29	96

выпуск 04.11.2026 № d6a6e5e88d · стр. 29 из 96

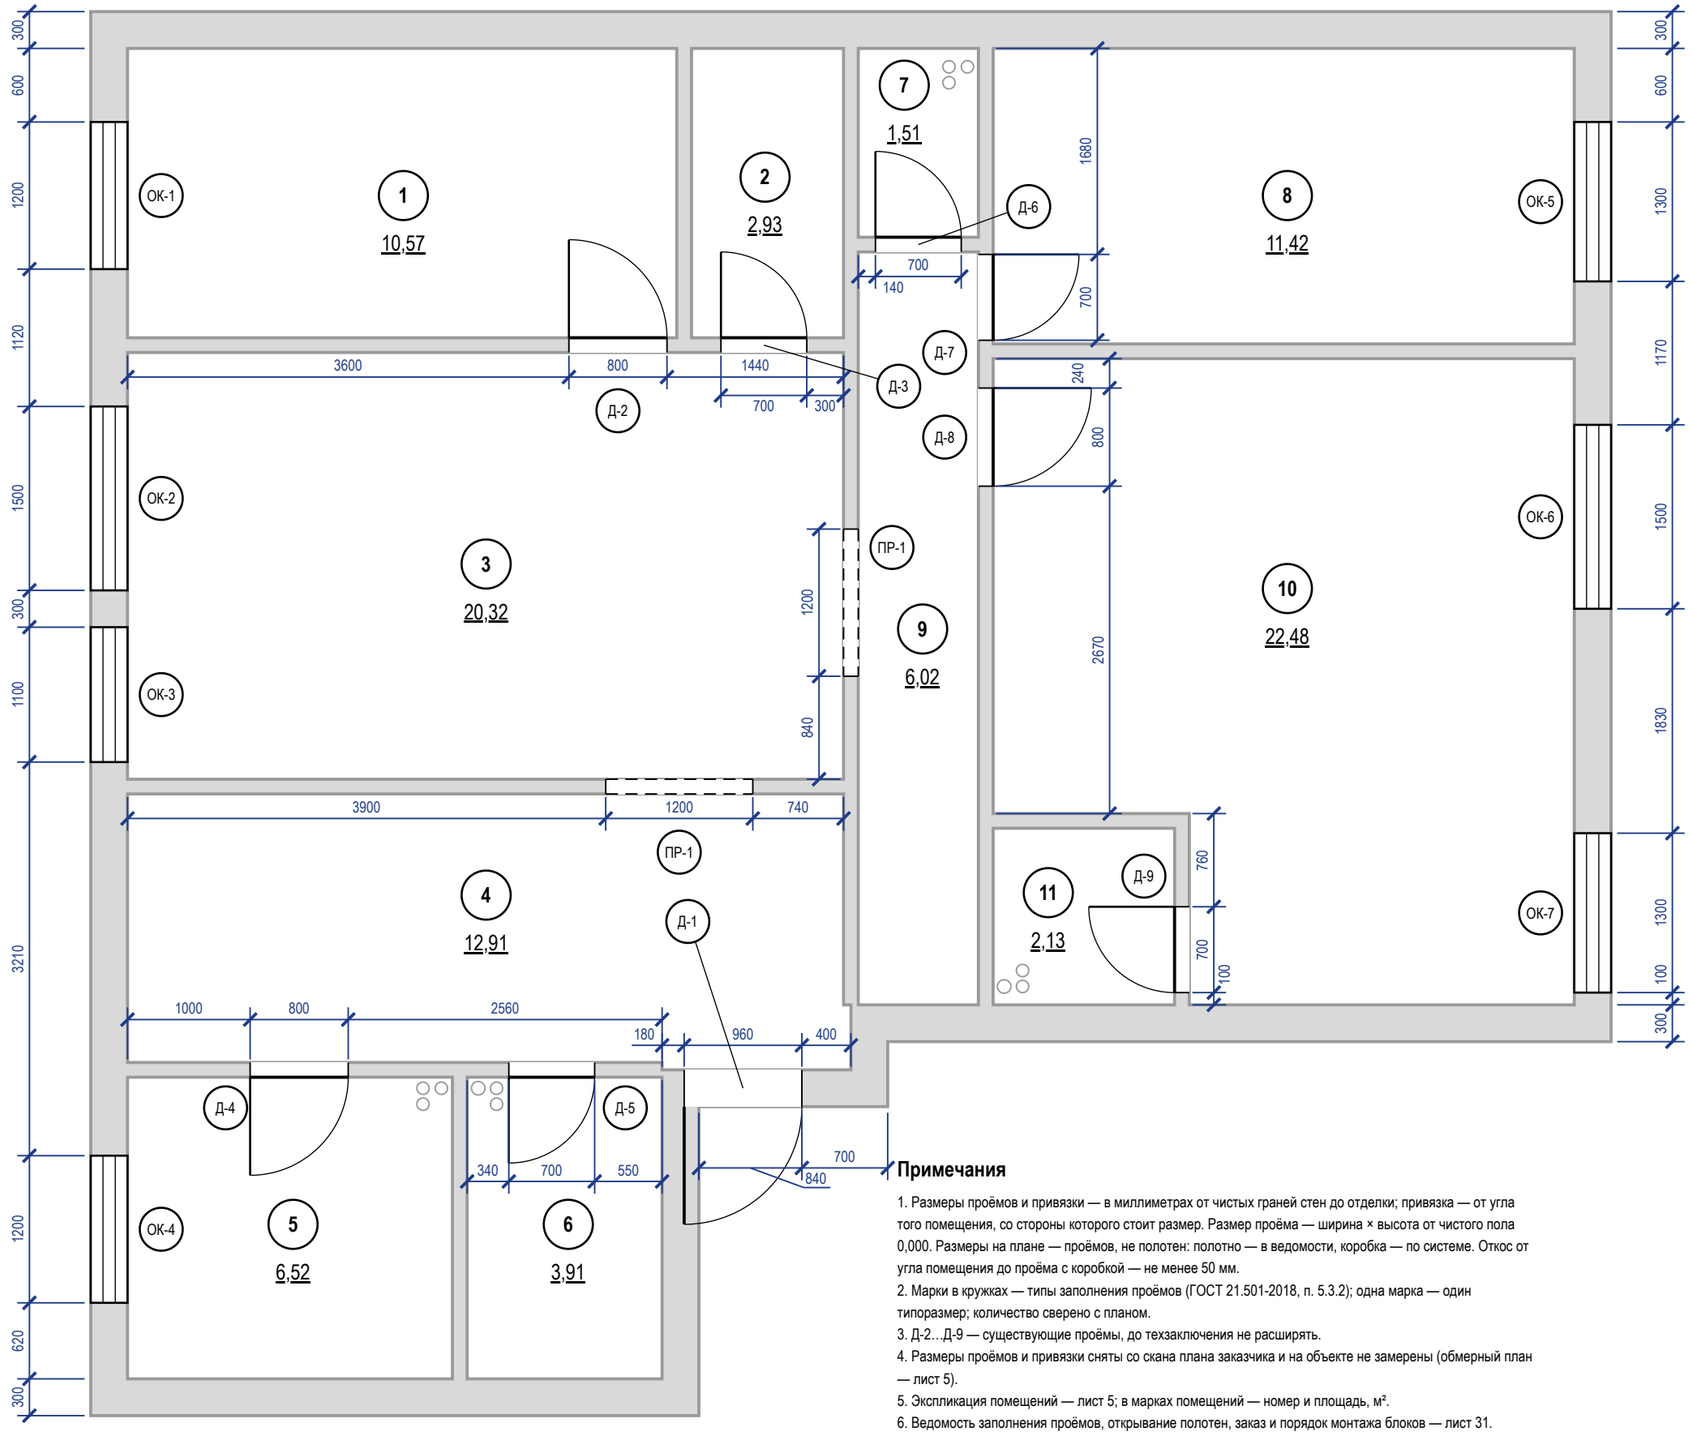

Примечания


1. Размеры проёмов и привязки — в миллиметрах от чистых граней стен до отделки; привязка — от угла того помещения, со стороны которого стоит размер. Размер проёма — ширина × высота от чистого пола 0,000. Размеры на плане — проёмов, не полотен: полотно — в ведомости, коробка — по системе. Откос от угла помещения до проёма с коробкой — не менее 50 мм.
2. Марки в кружках — типы заполнения проёмов (ГОСТ 21.501-2018, п. 5.3.2); одна марка — один типоразмер; количество сверено с планом.
3. Д-2…Д-9 — существующие проёмы, до техзаключения не расширять.
4. Размеры проёмов и привязки сняты со скана плана заказчика и на объекте не замерены (обмерный план — лист 5).
5. Экспликация помещений — лист 5; в марках помещений — номер и площадь, м².
6. Ведомость заполнения проёмов, открывание полотен, заказ и порядок монтажа блоков — лист 31.
7. Привязка проёма к углу помещения меньше 1 мм на листе, размер на плане не показан: Д-7 — 30 мм.

					Проект: Квартира 103 м²	М 1:50
	Лист	№ док.	Подпись	Дата		
Дизайнер	Кырлан А.С.			04.11.26	План размещения дверей	Стадия / Лист / Листов
						П / 30 / 96


Ведомость заполнения проёмов

Марка	Наименование, обозначение	Проём ш×в, мм	Полотно (расч.)	Кол.	Откр.	Отделка полотна	Фурнитура	Прим.
Д-1	Блок дверной входной, ГОСТ 31173-2016	960×2100	блок задать	1	Л	в комплекте блока	в комплекте блока (замки, глазок)	наружу
Д-2	Дверь скрытого монтажа, UNION FILO-60 Piatto	800×2100	700×2000	1	П	окраска No. 291 с двух сторон	скрытые петли 3D, магнитный замок	
Д-3	Дверь скрытого монтажа, UNION FILO-60 Piatto	700×2100	600×2000	1	П	S 0502-Y — пом. 2, No. 291 — пом. 3	скрытые петли 3D, магнитный замок	
Д-4	Дверь скрытого монтажа, UNION FILO-60 Piatto	800×2100	700×2000	1	Л	окраска No. 291 с двух сторон	скрытые петли 3D, магнитный замок	
Д-5	Дверь скрытого монтажа, UNION FILO-60 Piatto	700×2100	600×2000	1	Л	в тон облицовки — пом. 6, No. 291 — пом. 4	скрытые петли 3D, магнитный замок, фиксатор WC	порог 15
Д-6	Дверь скрытого монтажа, UNION FILO-60 Piatto	700×2100	600×2000	1	П	S 0502-Y — пом. 7, No. 291 — пом. 9	скрытые петли 3D, магнитный замок	
Д-7	Дверь скрытого монтажа, UNION FILO-60 Piatto	700×2100	600×2000	1	П	окраска No. 291 с двух сторон	скрытые петли 3D, магнитный замок	
Д-8	Дверь скрытого монтажа, UNION FILO-60 Piatto	800×2100	700×2000	1	П	окраска No. 291 с двух сторон	скрытые петли 3D, магнитный замок	
Д-9	Дверь скрытого монтажа, UNION FILO-60 Piatto	700×2100	600×2000	1	Л	в тон облицовки — пом. 11, No. 291 — пом. 10	скрытые петли 3D, магнитный замок, фиксатор WC	порог 15
ПР-1	Портал без заполнения	1200×2100		2				пом. 3; б/п
ОК-1	Блок оконный, ГОСТ 23166-2021; стекло — триплекс	1200×1560		1				низ 720
ОК-2	Блок оконный, ГОСТ 23166-2021; стекло — триплекс	1500×1550		1				низ 735
ОК-3	Блок оконный, ГОСТ 23166-2021; стекло — триплекс	1100×1550		1				низ 735
ОК-4	Блок оконный, ГОСТ 23166-2021; стекло — триплекс	1200×1550		1				низ 763
ОК-5	Блок оконный, ГОСТ 23166-2021; стекло — триплекс	1300×1552		1				низ 783
ОК-6	Блок оконный, ГОСТ 23166-2021; стекло — триплекс	1500×1548		1				низ 825
ОК-7	Блок оконный, ГОСТ 23166-2021; стекло — триплекс	1300×1548		1				пом. 10; низ 825


Схемы дверных блоков (1:50) — вид со стороны открывания; вершина треугольника — сторона петель

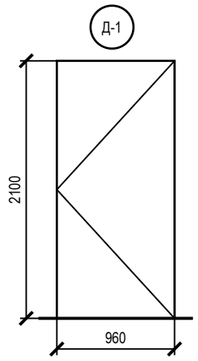


блок — по ГОСТ 31173
откр. Л

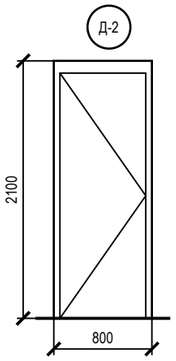


полотно 700×2000 (расч.)
откр. П

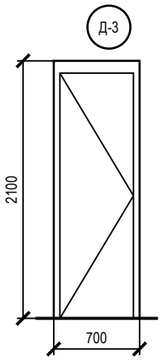


полотно 600×2000 (расч.)
откр. П

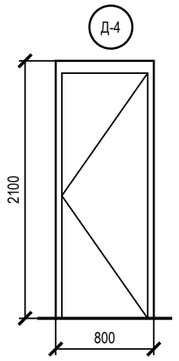


полотно 700×2000 (расч.)
откр. Л

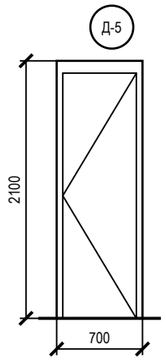


полотно 600×2000 (расч.)
откр. Л

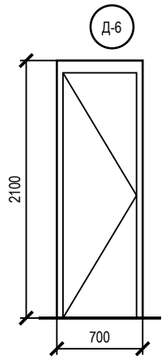


полотно 600×2000 (расч.)
откр. П

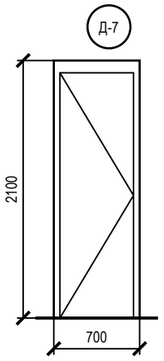


полотно 600×2000 (расч.)
откр. П

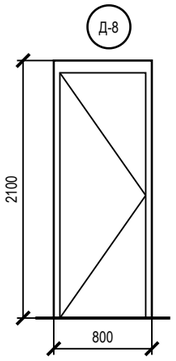

полотно 700×2000 (расч.)
откр. П

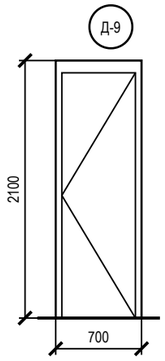

полотно 600×2000 (расч.)
откр. Л

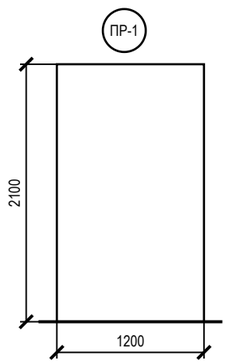


без заполнения

Примечания

1. Марки проёмов — те же, что на плане размещения дверей (лист 30); привязки проёмов — там же.
2. Открывание: Л — петли слева, П — справа, если смотреть со стороны, куда открывается полотно (на себя).
3. Остекление окон: ОК-1 (пом. 1) — триплекс; ОК-2 (пом. 3) — триплекс; ОК-3 (пом. 3) — триплекс; ОК-4 (пом. 5) — триплекс; ОК-5 (пом. 8) — триплекс; ОК-6 (пом. 10) — триплекс; ОК-7 (пом. 10) — триплекс. Тип стекла указать при заказе оконных блоков; замена на другое стекло — только по согласованию с автором проекта.
4. ОК-1, ОК-2, ОК-3, ОК-4, ОК-5, ОК-6, ОК-7: низ остекления 720 и 735 и 763 и 783 и 825 мм — ниже 900 мм от чистого пола, поэтому окно заказывать с безопасным стеклом (триплекс); ограждение проёма в проекте не задано (СП 54.13330.2022, п. 6.4.9; ГОСТ Р 56926).
5. Скрытые двери (Д-2…Д-9): проём замерить в чистоте; блок заказать до штукатурки (≈ 30 дн.), короб ставить до штукатурки; полотно навесить после чистовой отделки, красить в цвет стен. Порядок — практика монтажа, изготовитель подтверждает.
6. Полотно «расч.» — по проёму и ряду изделия с запасом по каталогам, заказ — по таблице проёмов модели; Д-2…Д-9: проём 2100, а под полотно 2000 по каталогам нужен 2050–2080, под 2100 — 2150–2180: высоту проёма — по модели; Д-1: входной блок по ГОСТ 31173-2016 — задать при выборе блока.

					Проект: Квартира 103 м²
	Лист	№ док.	Подпись	Дата	Ведомость заполнения проёмов
Дизайнер	Кырлан А.С.			04.11.26	

Стадия	Лист	Листов
П	31	96

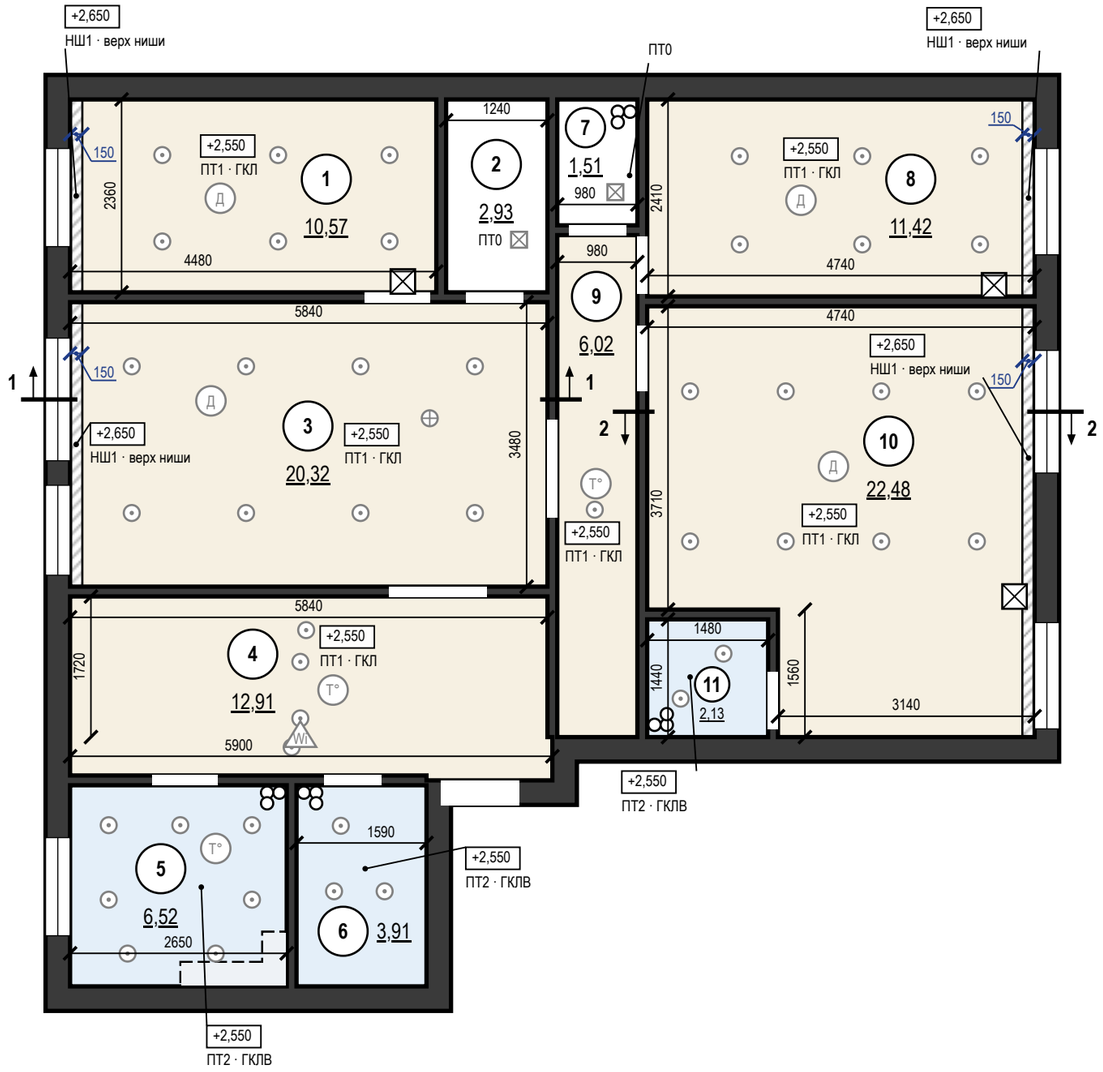

Ведомость потолков

Пом.	Марка	Конструкция	Низ / верх ниши	S, м²	Q
1	ПТ1	ГКЛ П113	+2,550	10,22	Q3
1	НШ1	ниша под шторы 150×100	+2,650	0,35	
2, 7	ПТ0	Существующий потолок, окраска	+2,650	4,44	
3	ПТ1	ГКЛ П113	+2,550	19,80	Q3
3	НШ1	ниша под шторы 150×100	+2,650	0,52	
4	ПТ1	ГКЛ П113	+2,550	12,91	Q3
5	ПТ2	ГКЛВ П113	+2,550	6,52	Q3
6	ПТ2	То же	+2,550	3,91	Q3
8	ПТ1	ГКЛ П113	+2,550	11,06	Q3
8	НШ1	ниша под шторы 150×100	+2,650	0,36	
9	ПТ1	ГКЛ П113	+2,550	6,02	Q3
10	ПТ1	То же	+2,550	21,69	Q3
10	НШ1	ниша под шторы 150×100	+2,650	0,79	
11	ПТ2	ГКЛВ П113	+2,550	2,13	Q3
		Итого		**100,72**	


Примечания

1. За отметку ±0,000 принят уровень чистого пола сухих помещений (готовое покрытие), а не существующего пола; пол пом. 6, 11 — −0,015; верх плиты перекрытия −0,064 — расчётный по пирогу пола, не замерен; существующий пол снимается до плиты, его отметка не замерена. Отметки в прямоугольниках — низ потолка; низ перекрытия +2,650. Марка потолка — одна конструкция и отметка на весь альбом.
2. Размеры помещений в свету (ширина × длина, мм), не поместившиеся на плане: пом. 2 — 1240 × 2360; пом. 4 — 5840 × 1720, 5900 × 470, 1540 × 60; пом. 5 — 2650 × 2460; пом. 6 — 1590 × 2460; пом. 7 — 980 × 1540; пом. 9 — 980 × 6140.
3. Потолки ГКЛ — каркасная система П113: подвесы через 1000 (с запасом: СП 163, табл. 14 — до 1100 при 0,15 кН/м²), несущие профили через 500, основные через 1200 мм; листы — поперёк несущих профилей. В помещениях 5, 6, 11 — ГКЛВ на оцинкованном каркасе.
4. Ниши под шторы 150×100 мм — на всю длину стены с окном; карниз — на закладной до обшивки (узел 1, лист 33).
5. Примыкание к стенам: теневой шов 15 мм, техзазор 3 мм — пом. 1, 3, 4, 5, 8, 9, 10, по стенам, выровненным штукатуркой (узел 1); пом. 6, 11 — разделительная лента.
6. Светильники и потолочные устройства — подложка с планов освещения, слаботочных систем и вентиляции (положение — по ним); вырезы и закладные — по ведомости на листе, до обшивки; отверстия не совмещать с профилями, глубина корпуса светильника до 70 мм.
7. Разрезы 1–1, 2–2 — на листе 33; высоты мебели и дверных блоков сверены с низом потолка в разрезах.
8. Шпаклевание ГКЛ и условия приёмки — Q3: рассеянный дневной свет, осмотр с 2 м; боковой свет не оценивается.
9. Ведомость вырезов и закладных в потолке — на листе 34; вырезы и закладные — до обшивки.
10. Пом. 5: короб воздуховода кухонной вытяжки ГКЛ 300×130 мм (ширина от стены × высота), низ +2,520, длина 1,37 м — по трассе плана вентиляции, вдоль стен до входа в канал; под плоский воздуховод 200×60 (сечение ≈ Ø125): круглый Ø125 в коробе 200 мм опустил бы кухню ниже 2,5 м — сечение подтверждает раздел ОВ; каркас ПН 28×27 по стене и плите, ПП 60×27, лист ГКЛ 12,5.
11. Люки ревизии 300×300 мм — по центру блоков питания LED (БП2, БП5, БП6; координаты — план освещения).
12. ПТ0 — пом. 2, 7: существующий потолок, окраска, без подвесного потолка, низ +2,650; материал и цвет — по ведомости отделки.
13. Сечения потолков М 1:10: пом. 1 — 1.1, 1.2 (лист 35); пом. 3 — 1.1, 1.2 (лист 35); пом. 8 — 1.1, 1.2 (лист 35); пом. 10 — 1.1, 1.2 (лист 35).

					Проект: Квартира 103 м² — **М 1:75**
	Лист	№ док.	Подпись	Дата	План потолков — Стадия: П; Лист: 32; Листов: 96
Дизайнер	Кырлан А.С.			04.11.26	


Разрез 1–1 (М 1:40)

Пом. 3 Гостиная-столовая; линия разреза — план потолков, лист 32

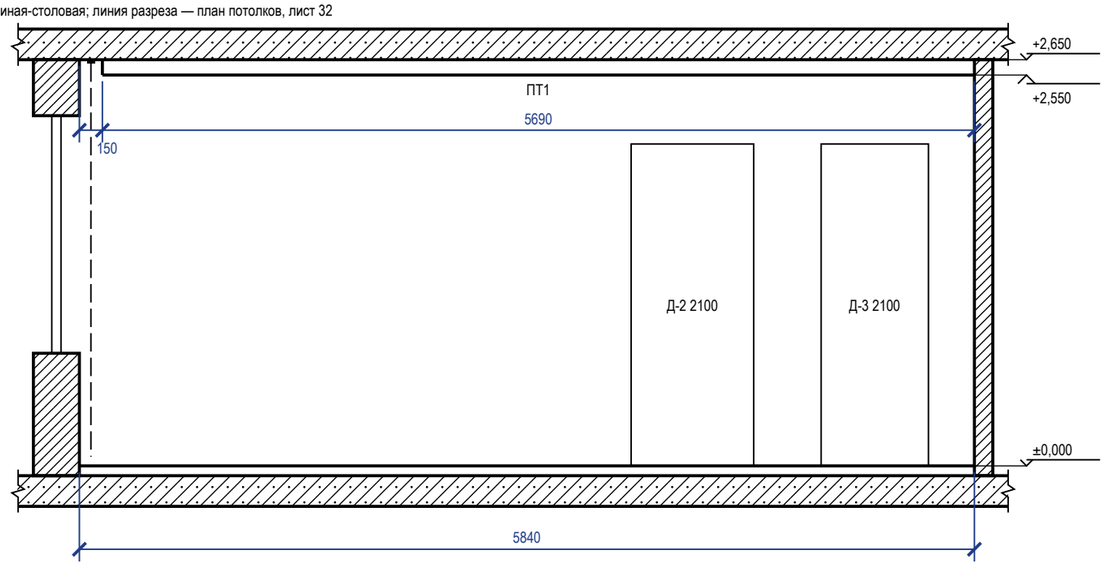


Разрез 2–2 (М 1:40)

Пом. 10 Спальня мастер; линия разреза — план потолков, лист 32

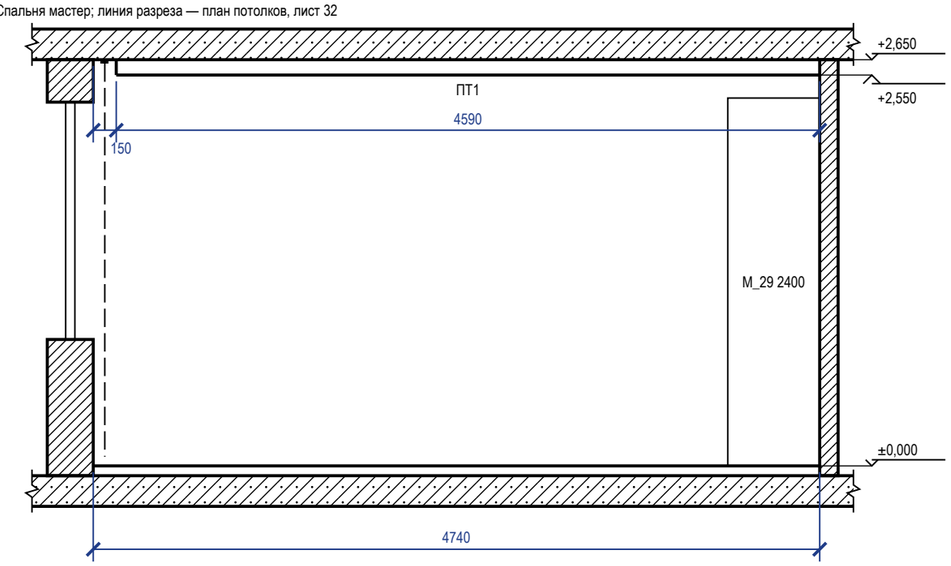

1 Ниша под шторы (М 1:10)

Пом. 1, 3, 8, 10; без подсветки; закладные под карниз — до обшивки

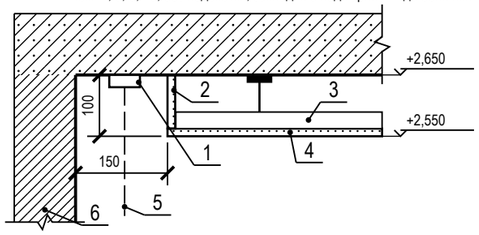

1 — карниз (шина), высота с верхом портьеры 80 мм
2 — стенка ниши — ГКЛ 12,5
3 — ПП 60×27 — каркас короба
4 — низ короба нижнего уровня — ГКЛ 12,5
5 — портьера
6 — стена с окном

Условные обозначения

- плита перекрытия в сечении
- стена в сечении
- потолок ГКЛ в сечении; под линией — марка потолка (план потолков)
- мебель и дверные проёмы за секущей плоскостью; число — марка и верх от чистого пола, мм
- портьера в нише под шторы

Примечания

1. Разрезы — по линиям 1–1, 2–2 на плане потолков (лист 32). Отметки — от ±0,000 чистого пола, м; размеры — мм.
2. Высоты мебели и дверных блоков за секущей плоскостью сверены с низом потолка над ними: верх ниже низа короба и поля.
3. ГКЛ 12,5 мм по каркасу П113. Ниша под шторы — на всю длину стены с окном, карниз на закладной до обшивки (узел 1 — на этом листе).
4. Толщины плит перекрытия и пирога пола показаны условно.
5. Сечения потолков по помещениям М 1:10 (отметки помещения, профили, подвесы, крепёж, изделия) — лист 35.
6. Ведомость объёмов потолков (лист ГКЛ, профиль, подвесы, лента, блоки питания, люки) — на листе 34.

					Проект: Квартира 103 м²	**М 1:40; 1:10**
	Лист	№ док.	Подпись	Дата		
Дизайнер	Кырлан А.С.			04.11.26	Разрезы и узлы потолков	Стадия: П; Лист: 33; Листов: 96

Ведомость объёмов потолков

Позиция	Ед.	Кол.	Пом.
Лист ГКЛ 12,5	м²	85,08	1, 3, 4, 8, 9, 10
Лист ГКЛВ 12,5	м²	12,56	5, 6, 11
Борта и карнизы (входят в площади листов выше)	м²	1,36	1, 3, 8, 10
Профиль ПП 60×27	м	276,03	1, 3, 4, 5, 6, 8, 9, 10, 11
Профиль ПН 28×27	м	148,38	1, 3, 4, 5, 6, 8, 9, 10, 11
Подвес прямой	шт.	84	1, 3, 4, 5, 6, 8, 9, 10, 11
Анкер-клин к плите	шт.	84	1, 3, 4, 5, 6, 8, 9, 10, 11
Шуруп TN 3,5×25	шт.	2246	1, 3, 4, 5, 6, 8, 9, 10, 11
Лента армирующая для швов	м	117,17	1, 3, 4, 5, 6, 8, 9, 10, 11
Шпаклёвка для швов	кг	39,06	1, 3, 4, 5, 6, 8, 9, 10, 11
Грунтовка (швы)	л	9,76	1, 3, 4, 5, 6, 8, 9, 10, 11
Лента разделительная по периметру	м	121,34	1, 3, 4, 5, 6, 8, 9, 10, 11
Сплошная шпаклёвка и окраска (площадь развёртки)	м²	97,64	1, 3, 4, 5, 6, 8, 9, 10, 11
Люк ревизии	шт.	3	1, 8, 10

Ведомость вырезов и закладных в потолке

Марка	Устройство	Кол.	Пом.
	Светильник встраиваемый (марки — план освещения)	46	1, 3, 4, 5, 6, 8, 9, 10, 11
	Светильник накладной (марки — план освещения)	2	2, 7
	Светильник подвесной (марки — план освещения)	1	3
ИП2, ИП1, ИП7, ИП8	Извещатель дымовой	4	1, 3, 8, 10
ИП3, ИП4, ИП6	Извещатель тепловой	3	4, 5, 9
AP1	Точка доступа Wi-Fi, PoE	1	4
	Люк ревизии 300×300	3	1, 8, 10

Примечания


1. ГКЛ 12,5 мм по каркасу П113; узлы коробов и ниш под шторы: узел 1 — лист 33; условные обозначения разрезов — на листе 33.
2. Ведомость вырезов и закладных в потолке — к плану потолков (лист 32): вырезы и закладные — до обшивки, марки светильников — по плану освещения.
3. Ведомость объёмов — по геометрии плана потолков: Лист ГКЛ 12,5 — плоскости уровней + борта (без арочных участков); Лист ГКЛВ 12,5 — плоскости уровней + борта; Борта и карнизы — длина перепада × перепад; Профиль ПП 60×27 — S × (1/шаг несущ. + 1/шаг осн.) + стойки бортов; Профиль ПН 28×27 — периметр стен + 2 × перепады + карнизы; Подвес прямой — по раскладке: S уровня / (шаг осн. × шаг подвесов), пояс уже шага — ряд вдоль пояса, фигура — по контуру; шаг подвесов — не больше табл. 14 СП 163; Анкер-клин к плите — по одному на подвес (Knauf П113); Шуруп TN 3,5×25 — 23 шт./м² (Knauf П113, табл. 2 альбома П 11); Лента армирующая для швов — 1,2 м/м² листа (Knauf); Шпаклёвка для швов — 0,4 кг/м² листа, только швы (Knauf); Грунтовка (швы) — 0,1 л/м² листа, только швы (Knauf); Лента разделительная по периметру — периметр стен под потолком ГКЛ; Сплошная шпаклёвка и окраска (площадь развёртки) — плоскости + борта; расход — по паспорту материала (норма расхода на сплошной слой не подтверждена); Люк ревизии — план потолков; без запаса на подрезку (при закупке листа: ×1,075 при S > 20 м², ×1,175 — 10–20 м², ×1,275 — < 10 м²).

					Проект: Квартира 103 м²
	Лист	№ док.	Подпись	Дата	Разрезы и узлы потолков (продолжение)
Дизайнер	Кырлан А.С.			04.11.26	

Стадия	Лист	Листов
П	34	96

Сечение 1.1. Ниша под шторы (М 1:10)

Пом. 1 Кабинет-библиотека, 3 Гостиная-столовая, 8 Спальня 2, 10 Спальня мастер; без подсветки; закладные под карниз — до обшивки

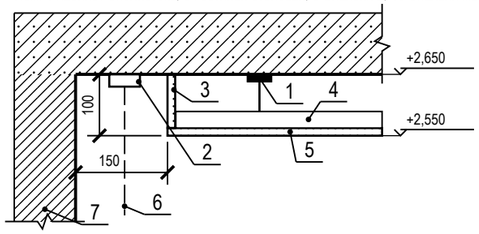

1 — анкер-клин к плите — по одному на подвес; подвес прямой, шаг 1000 мм

2 — карниз (шина), высота с верхом портьеры 80 мм

3 — стенка ниши — ГКЛ 12,5

4 — ПП 60×27 — каркас короба, основные через 1200 мм; соединители одноуровневые, шурупы LN 3,5×9


5 — низ короба нижнего уровня — ГКЛ 12,5; шурупы TN 3,5×25 через 170 мм

6 — портьера

7 — стена с окном

Сечение 1.2. Примыкание потолка к стене (М 1:10)

Пом. 1 Кабинет-библиотека, 3 Гостиная-столовая, 8 Спальня 2, 10 Спальня мастер; примыкание — теневой шов

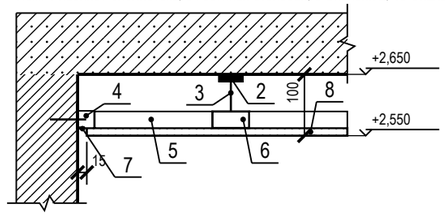

1 — плита перекрытия

2 — анкер-клин к плите — по одному на подвес

3 — подвес прямой, шаг 1000 мм

4 — ПН 28×27 по периметру — дюбель-гвоздь через ≤ 500 мм, не менее 3 на профиль

5 — ПП 60×27 несущий (вид) через 500 мм, в ПН

6 — ПП 60×27 основной (сечение) через 1200 мм; соединители одноуровневые, шурупы LN 3,5×9


7 — теневой профиль: шов 15 мм, зазор 3 мм; стена под шов выровнена

8 — ГКЛ 12,5 по П113; шурупы TN 3,5×25 через 170 мм

Примечания

1. Сечения потолков М 1:10 по помещениям с нишами LED и нишами под шторы: отметки и размеры этого помещения от ±0,000 чистого пола (м, мм). Положение — по плану потолков (лист 32): короб и ниша LED — по линиям ленты, ниша под шторы — у стены с окном; типовые узлы по группам помещений — на листе 33.
2. Крепёж: подвес прямой к плите на анкер-клине — по одному на подвес (Knauf П113); ПН к стенам — дюбель-гвоздь через ≤ 500 мм, не менее 3 на профиль (серия 1.045.9-2.08); лист 12,5 — шурупы TN 3,5×25 через 170 мм (СП 163, табл. 15); профили между собой — соединители одноуровневые, шурупы LN 3,5×9.
3. Изделие карниза, профиля LED и галтели подписано артикулом из данных; где артикул не выбран, сечение дано по габаритам из данных (ширина и глубина ниши, щель под свет), изделие подбирается по ним.

					Проект: Квартира 103 м²	**М 1:10**
	Лист	№ док.	Подпись	Дата		
Дизайнер	Кырлан А.С.			04.11.26	Сечения потолков М 1:10	Стадия / Лист / Листов
						П / 35 / 96

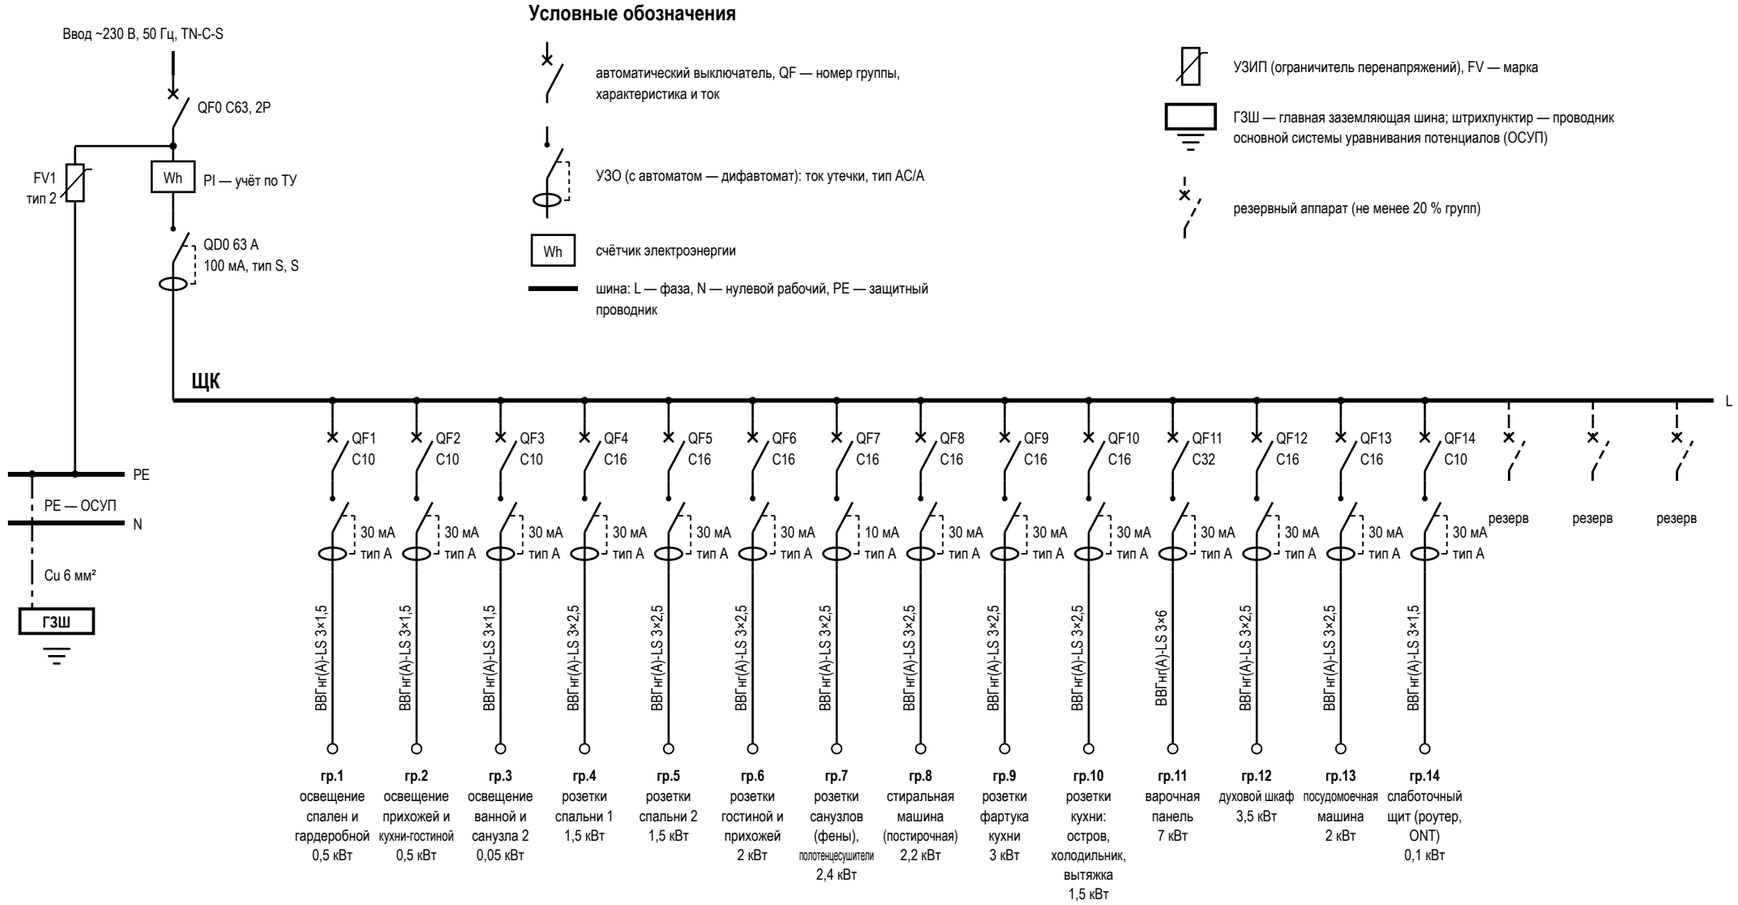

Условные обозначения

- автоматический выключатель, QF — номер группы, характеристика и ток
- УЗО (с автоматом — дифавтомат): ток утечки, тип AC/A
- Wh — счётчик электроэнергии
- шина: L — фаза, N — нулевой рабочий, PE — защитный проводник
- УЗИП (ограничитель перенапряжений), FV — марка
- ГЗШ — главная заземляющая шина; штрихпунктир — проводник основной системы уравнивания потенциалов (ОСУП)
- резервный аппарат (не менее 20 % групп)

Данные щитка

Показатель	Значение
Номер щитка	ЩК
Тип	ЩРВ-П-24, IP41
Уст. мощность, кВт	27,75
Разреш. мощность, кВт	15
Расчётная, кВт	9,8
Автоматы 1п: занят. / рез.	14 / 3
Модулей: всего / занято	24 / 20
Ток на вводе, А	63
Вводной аппарат	QF0 C63, 2P
УЗИП	FV1, тип 2, ЩК, после счётчика
ГЗШ, проводник ОСУП	Cu 6 мм²


Таблица групп щита ЩК и кабельный журнал

№	Назначение	Помещения	Автомат	УЗО / дифавтомат	Кабель	Длина, м	P, кВт	Точек
1	освещение спален и гардеробной	1, 2, 3, 5, 7, 8, 10	C10	30 мА, тип A	ВВГнг(A)-LS 3×1,5	173,6	0,5	63
2	освещение прихожей и кухни-гостиной	4, 9	C10	30 мА, тип A	ВВГнг(A)-LS 3×1,5	41	0,5	11
3	освещение ванной и санузла 2	4, 6, 10, 11	C10	30 мА, тип A	ВВГнг(A)-LS 3×1,5	53,3	0,05	11
4	розетки спальни 1	10	C16	30 мА, тип A	ВВГнг(A)-LS 3×2,5	33	1,5	4
5	розетки спальни 2	1, 3, 8	C16	30 мА, тип A	ВВГнг(A)-LS 3×2,5	75,2	1,5	15
6	розетки гостиной и прихожей	4, 9	C16	30 мА, тип A	ВВГнг(A)-LS 3×2,5	26,2	2	3
7	розетки санузлов (фены), полотенцесушители	6, 11	C16	10 мА, тип A	ВВГнг(A)-LS 3×2,5	30	2,4	4
8	стиральная машина (постирочная)	7	C16	30 мА, тип A	ВВГнг(A)-LS 3×2,5	20	2,2	1
9	розетки фартука кухни	5	C16	30 мА, тип A	ВВГнг(A)-LS 3×2,5	16,6	3	2
10	розетки кухни: остров, холодильник, вытяжка	5	C16	30 мА, тип A	ВВГнг(A)-LS 3×2,5	19	1,5	4
11	варочная панель	5	C32	30 мА, тип A	ВВГнг(A)-LS 3×6	15,8	7	1
12	духовой шкаф	5	C16	30 мА, тип A	ВВГнг(A)-LS 3×2,5	35,3	3,5	1
13	посудомоечная машина	5	C16	30 мА, тип A	ВВГнг(A)-LS 3×2,5	53	2	1
14	слаботочный щит (роутер, ONT)	4	C10	30 мА, тип A	ВВГнг(A)-LS 3×1,5	3,5	0,1	1
	Итого по сечениям ВВГнг(A)-LS, м: 3×1,5 — 271,4; 3×2,5 — 308,3; 3×6 — 15,8					595,5		

Примечания

1. Схема однолинейная: одна линия — фаза, N и PE группы; аппараты — в отключённом положении (ГОСТ 2.702, ГОСТ 2.755). Номера групп — как у точек на планах (гр.). За отметку 0,000 принят уровень чистого пола; высота щита — по плану розеток.
2. Розеточные и мокрые линии — через УЗО или дифавтомат с током утечки не более 30 мА (ПУЭ 7.1.79); в санузле выполнить ДСУП (ПУЭ 7.1.87–7.1.88).
3. УЗО тип A — для линий с электроникой, стиральной и посудомоечной машиной, LED-драйверами; тип AC — только для чисто активной нагрузки.
4. Кабель — медный, исполнение нг(A)-LS (ГОСТ 31565-2012); скрытая прокладка только горизонтально и вертикально, фактические трассы зафиксировать исполнительной схемой до закрытия отделкой.
5. Номинал автомата — не выше допустимого тока кабеля: 1,5 мм² — до 10 А, 2,5 мм² — до 16 А. Резерв щита — не менее 20 % модулей.
6. Расчёт нагрузок, токов КЗ, селективности и сечений — по проекту ЭОМ организации с допуском СРО; лист задаёт состав, расположение и группы.
7. УЗИП FV1 — после вводного автомата, проводник к шине PE — кратчайший, без петель. Шина PE щита соединяется с ГЗШ проводником ОСУП; к ГЗШ присоединяются трубы водопровода и отопления на вводе в квартиру (ПУЭ 7.1.87). Шины N и PE — раздельные, после разделения PEN не объединяются.
8. До подключения нагрузки — приёмо-сдаточные испытания с протоколом: сопротивление изоляции линий не менее 0,5 МОм, срабатывание УЗО по току и времени, непрерывность защитных проводников PE (ПУЭ, гл. 1.8).

					Проект: Квартира 103 м²
	Лист	№ док.	Подпись	Дата	
Дизайнер	Кырлан А.С.			04.11.26	Однолинейная схема щита
					Стадия: П; Лист: 36; Листов: 96

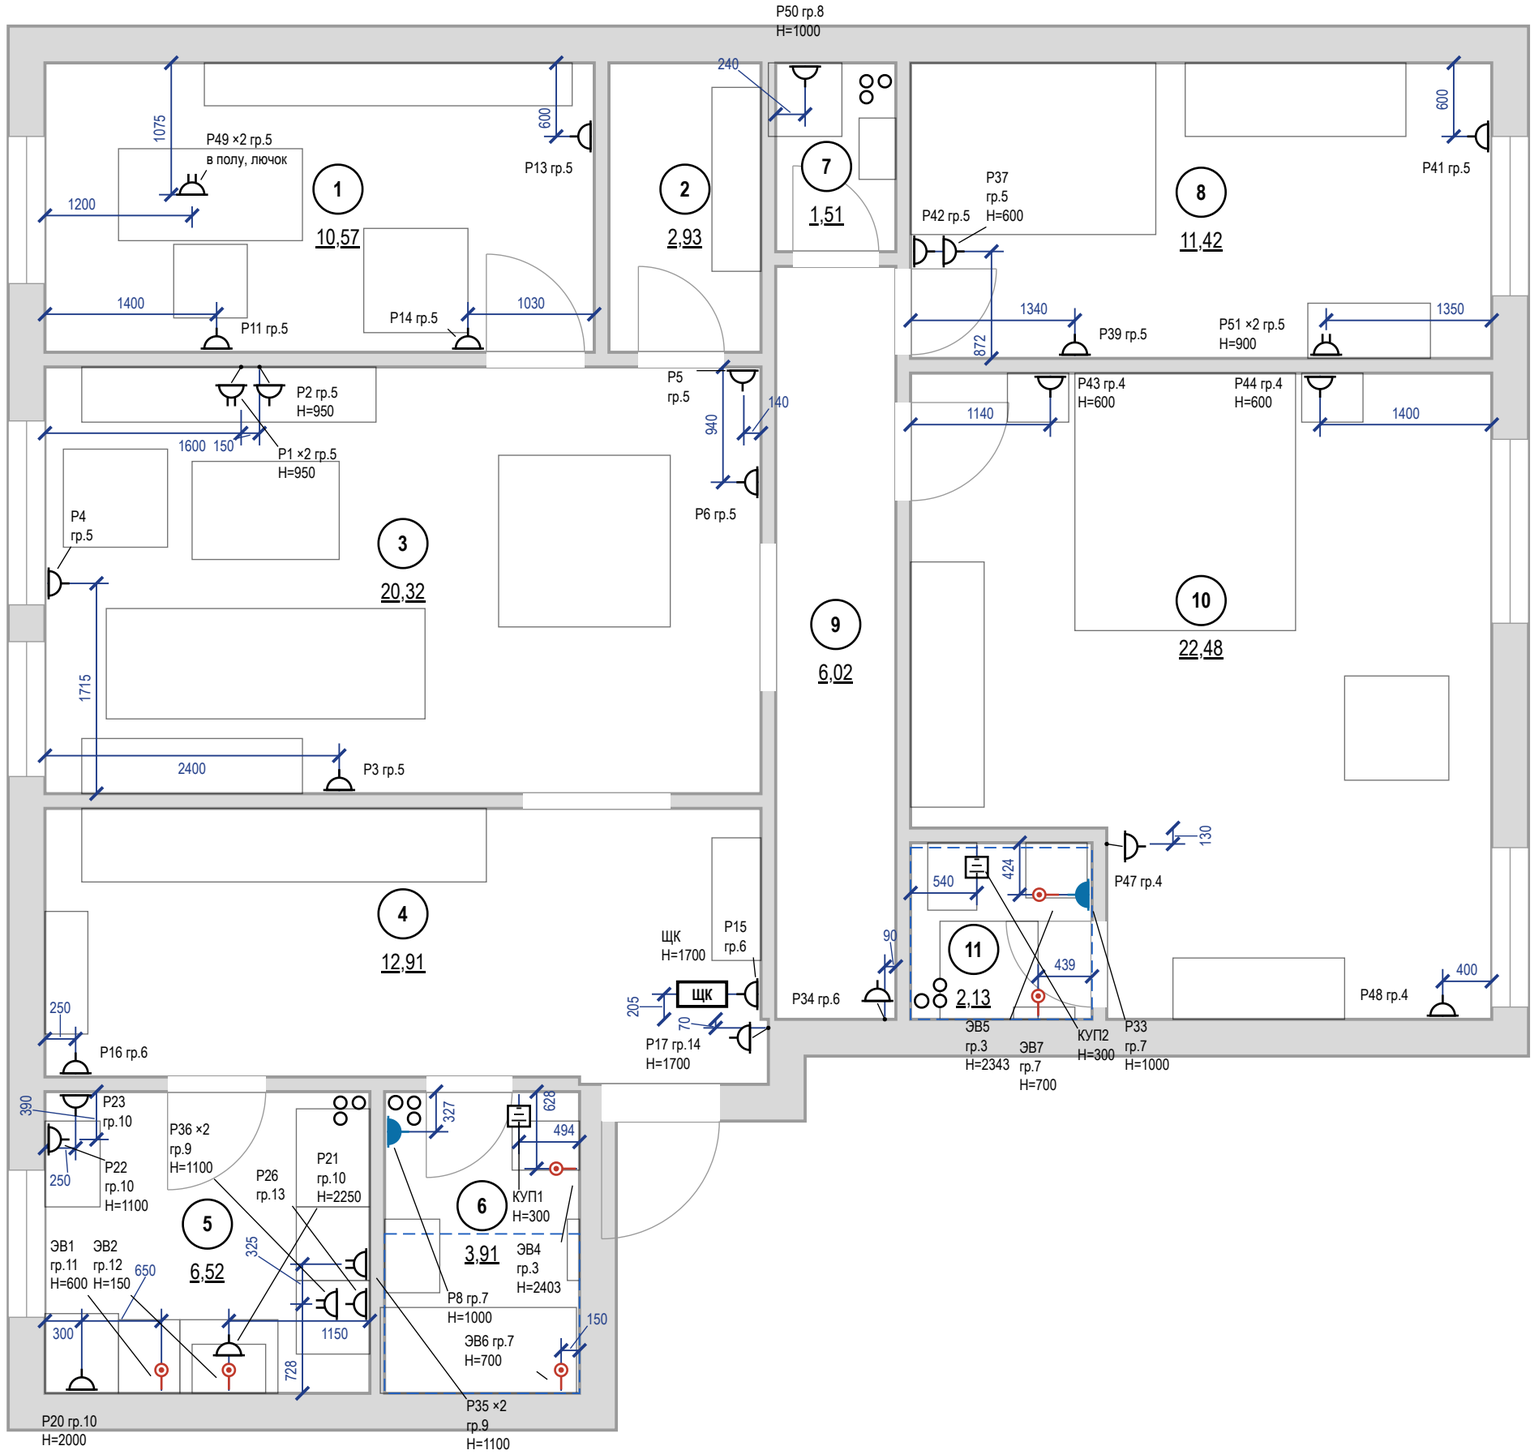

Условные обозначения

Знак	Тип изделия	H, мм	Кол., шт
	Розетка с заземлением	300	17
	То же	у знака	9
	Блок розеток с заземлением, рамка 2 поста	у знака	5
	Розетка с заземлением IP44	1000	2
	Вывод кабеля к прибору	у знака	6
	КУП (уравнивание потенциалов)	300	2
ЩК	Щит квартирный	1700	1

розетка с заземляющим контактом; у знака — марка, ×N — постов в рамке, гр. — группа щита, H — высота оси, мм

знак разведён для читаемости: точка на стене — у выноски, привязка — до неё

граница зоны 2 ванной (600 мм от ванны/поддона)

мебель и сантехприборы — подложка

стояк: К1 — канализация, В1 — ХВС, Т3 — ГВС


1 — номер помещения, площадь м²

Итого розеток (механизмов) — 38 шт; рамок — 33 шт: на 1 пост — 28, на 2 поста — 5.

Примечания

1. За отметку 0,000 принят уровень чистого пола. Высоты H — от чистого пола до оси изделия; привязки — от чистовой грани стены до оси механизма (у рамки на несколько постов — до оси рамки).
2. Розетки без отметки H у знака — на высоте 300 мм от чистого пола до оси механизма; выводы кабеля — по паспорту прибора.
3. Розетки в санузле — только вне зон 0–2 (ПУЭ 7.1.48, ГОСТ Р 50571.7.701-2024), IP44, через УЗО 30 мА.
4. Розеточные и мокрые линии — через УЗО или дифавтомат с током утечки не более 30 мА (ПУЭ 7.1.79); в санузле выполнить ДСУП (ПУЭ 7.1.87–7.1.88).
5. Кабель — медный, исполнение нг(А)-LS (ГОСТ 31565-2012); скрытая прокладка только горизонтально и вертикально, фактические трассы зафиксировать исполнительной схемой до закрытия отделкой.
6. Расчёт нагрузок, токов КЗ, селективности и сечений — по проекту ЭОМ организации с допуском СРО; лист задаёт состав, расположение и группы.
7. Выводы кухонной техники — после утверждения проекта кухни (ориентировочно); привязки выводов даны от осей модулей гарнитура и пересматриваются вместе с проектом кухни.
8. Электрический тёплый пол проектом не предусмотрен; при решении заказчика устроить — отдельный лист «План тёплых полов»: контуры с отступом 100 мм от стен и мебели без ножек, датчик в гофре, терморегулятор, своя группа щита через УЗО 30 мА.

					Проект: Квартира 103 м²	**М 1:50**
	Лист	№ док.	Подпись	Дата	План розеток и электровыводов	Стадия / Лист / Листов
Дизайнер	Кырлан А.С.			04.11.26		П / 37 / 96

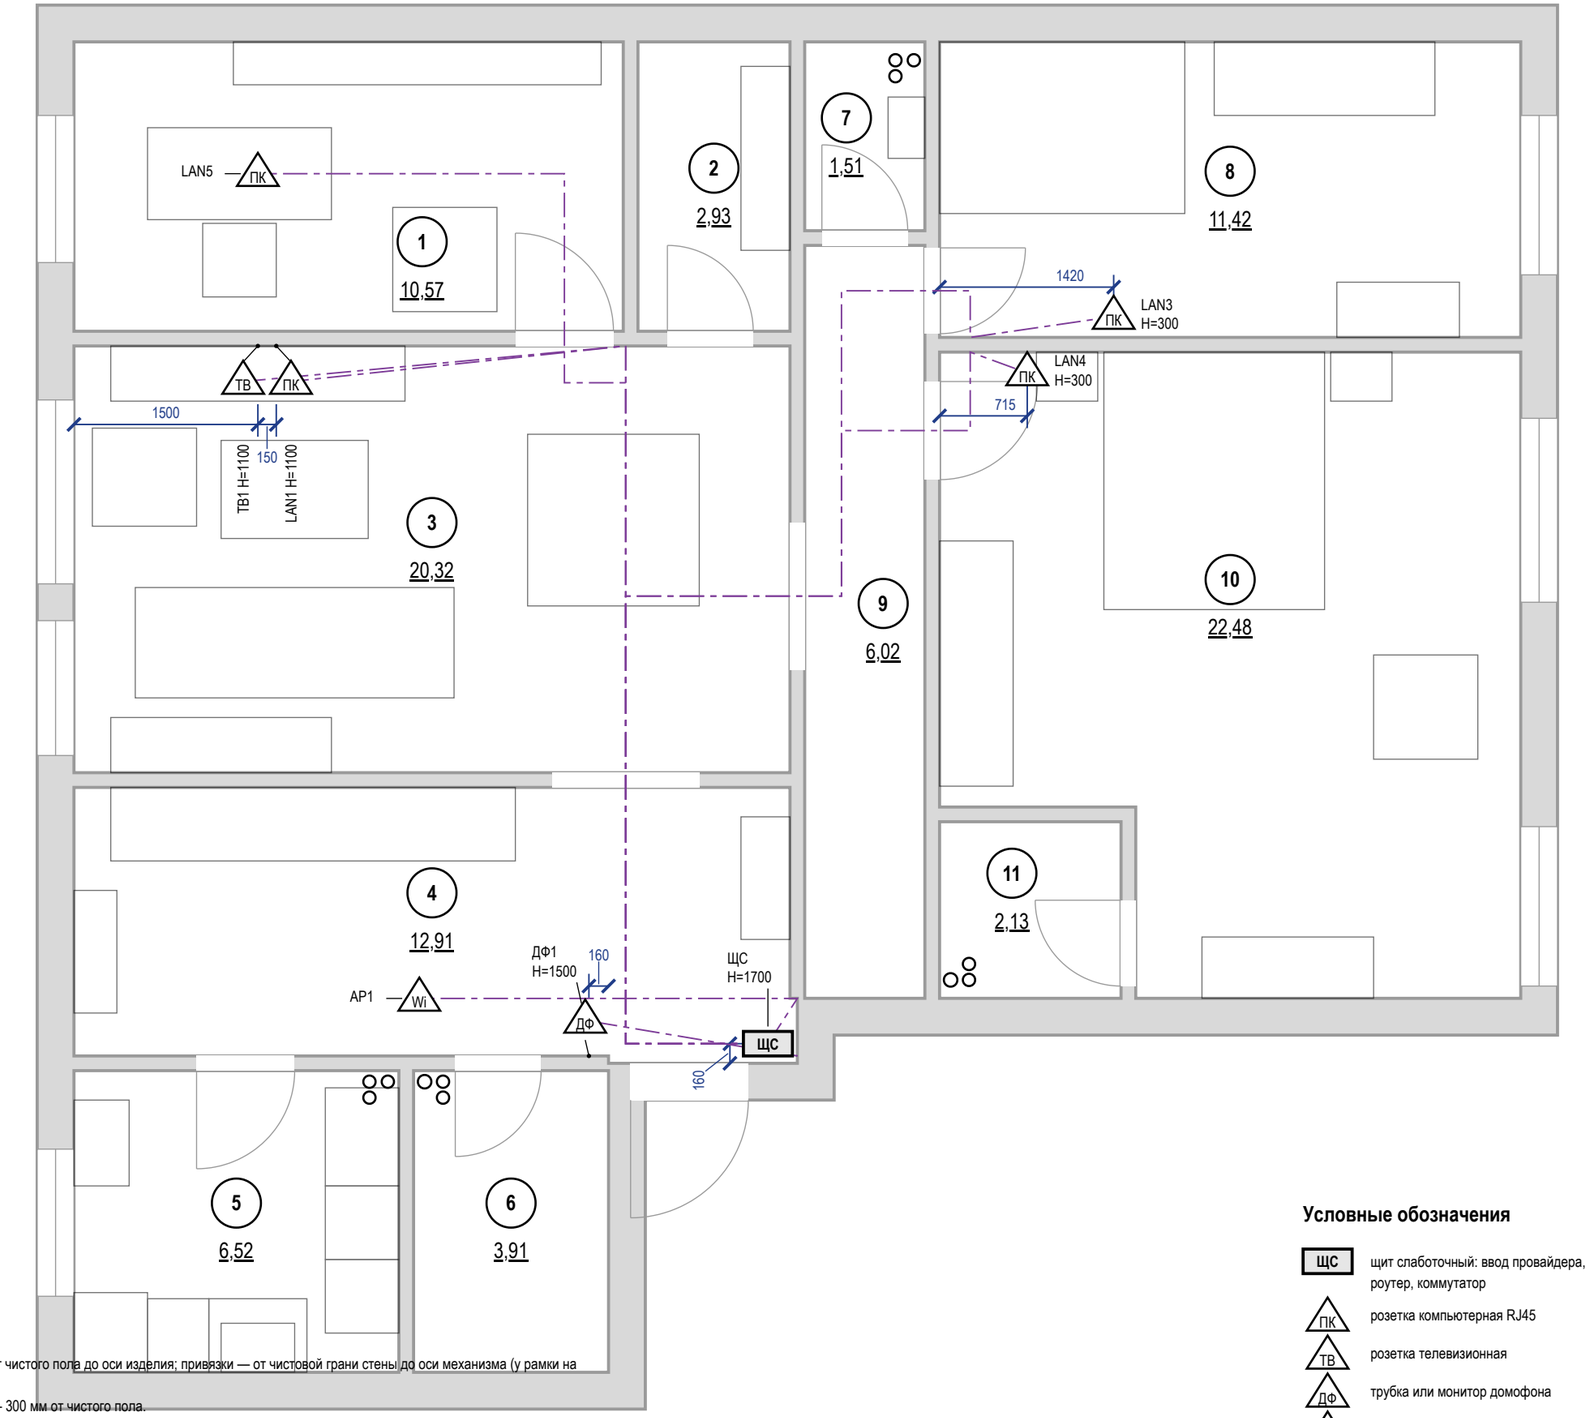


Примечания

1. За отметку 0,000 принят уровень чистого пола. Высоты H — от чистого пола до оси изделия; привязки — от чистовой грани стены до оси механизма (у рамки на несколько постов — до оси рамки).
2. Высота установки, не указанная на плане: розетки LAN и ТВ — 300 мм от чистого пола.
3. Слаботочные кабели — отдельно от силовых: в своей трубе или лотке, при параллельной прокладке не ближе 100 мм к силовым, пересечения под прямым углом; каждую точку — отдельным кабелем от ЩС без скруток.
4. Трассы на листе — принципиальные; фактические зафиксировать исполнительной схемой до закрытия отделкой. Силовые линии, УЗО 30 мА, ДСУП, кабель нг(A)-LS — по листам розеток и щита.
5. Проект силовой части и расчёт токов КЗ — по проекту ЭОМ; слаботочная часть согласуется с провайдером и управляющей компанией (домофон, коллективное ТВ).

Условные обозначения

- ЩС — щит слаботочный: ввод провайдера, роутер, коммутатор
- ПК — розетка компьютерная RJ45
- ТВ — розетка телевизионная
- ДФ — трубка или монитор домофона
- Wi — точка доступа Wi-Fi (питание PoE)
- кабель от ЩС до точки, отдельным лучом
- мебель и сантехприборы — подложка
- стояк: К1 — канализация, В1 — ХВС, Т3 — ГВС
- 1 — номер помещения, площадь м²

					Проект: Квартира 103 м²	М 1:50
	Лист	№ док.	Подпись	Дата	План слаботочных сетей	Стадия / Лист / Листов
Дизайнер	Кырлан А.С.			04.11.26		П / 38 / 96

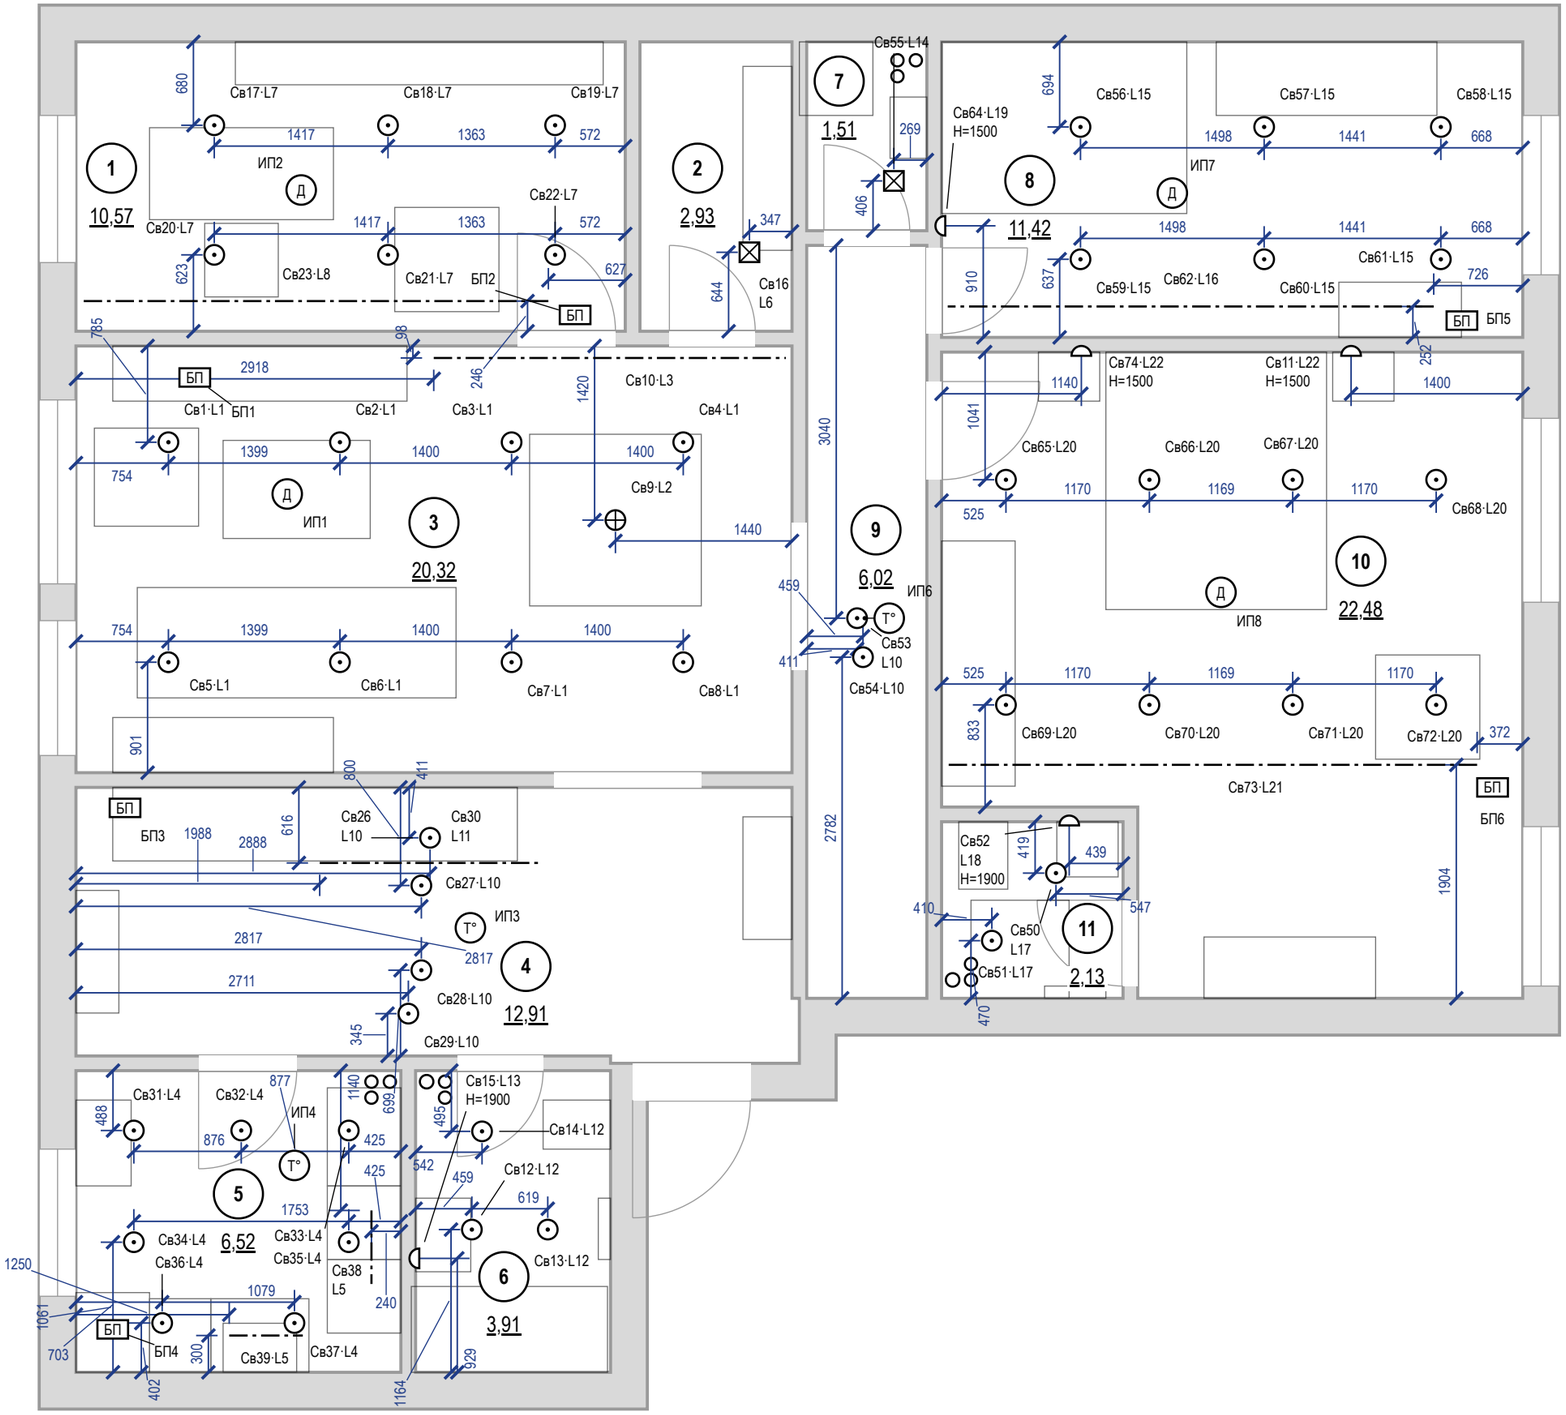

Условные обозначения

- светильник встраиваемый точечный
- светильник потолочный накладной
- светильник подвесной
- светильник настенный (бра), H — высота оси
- светодиодная лента в профиле / в карнизе короба
- Св1·L1 — марка светильника (как в ведомости и на развёртках) · группа включения L (лист 41)
- Д — извещатель пожарный дымовой автономный
- T° — извещатель пожарный тепловой
- БП — блок питания LED, с доступом (люк от 100×100 мм)
- мебель и сантехприборы — подложка
- стояк: К1 — канализация, В1 — ХВС, Т3 — ГВС
- 1 — номер помещения, площадь м²

Примечания

1. За отметку 0,000 принят уровень чистого пола. Высоты H — от чистого пола до оси изделия; привязки — от чистовой грани стены до оси механизма (у рамки на несколько постов — до оси рамки).
2. Высота установки, не указанная на плане: светильники — на потолке; настенные — по отметке H у знака. Привязки — до оси светильника от чистовой грани стены, по рядам.
3. Во влажных помещениях — светильники не ниже IP44; в зонах 0–2 ванной — по ГОСТ Р 50571.7.701-2024 (зона 1 — IPX5).
4. Розеточные и мокрые линии — через УЗО или дифавтомат с током утечки не более 30 мА (ПУЭ 7.1.79); в санузле выполнить ДСУП (ПУЭ 7.1.87–7.1.88).
5. Кабель — медный, исполнение нг(A)-LS (ГОСТ 31565-2012); скрытая прокладка только горизонтально и вертикально, фактические трассы зафиксировать исполнительной схемой до закрытия отделки.
6. Расчёт нагрузок, токов КЗ, селективности и сечений — по проекту ЭОМ организации с допуском СРО; лист задаёт состав, расположение и группы.
7. Ведомость светильников (тип, количество, мощность, поток, Тц, Ra) — лист 40.

					Проект: Квартира 103 м² — **М 1:50**
	Лист	№ док.	Подпись	Дата	План освещения
Дизайнер	Кырлан А.С.			04.11.26	Стадия: П · Лист: 39 · Листов: 96

Параметры светильников для подбора

Поз.	Марки	Наименование	Установка	Кол.	P, Вт	Σ P, Вт	Ф, лм	Тц, К	Ra	Угол, °	IP	Дим.	Слой	Группа	Пом.
1	Св17–Св22, Св56–Св61	Встраиваемый точечный	в ГКЛ, корпус ≤ 70 мм	12	12	144	1050	2700	90	—	20	—	общий	L7, L15	1, 8
2	Св23, Св62	Лента светодиодная 24 В	на поверхности, профиль с рассеивателем	24,6 м	9,6/м	236,2	900/м	2700	90	—	20	да	акцентный	L8, L16	1, 8
3	Св16, Св55	Потолочный накладной	на потолке, засветка стены	2	10	20	900	3000	90	—	20	—	общий	L6, L14	2, 7
4	Св1–Св8, Св31–Св37	Встраиваемый точечный	в ГКЛ, корпус ≤ 70 мм	15	12	180	1000	3000	90	—	20	—	общий	L1, L4	3, 5
5	Св9	Подвесной	подвес, низ H=1600	1	15	15	1200	2700	90	—	20	—	рабочий	L2	3
6	Св10	Лента светодиодная 24 В	на поверхности, профиль с рассеивателем	5,4 м	9,6/м	51,8	900/м	2700	90	—	20	да	акцентный	L3	3
7	Св26–Св29, Св53, Св54	Встраиваемый точечный	в ГКЛ, корпус ≤ 70 мм	6	7	42	600	3000	90	—	20	—	общий	L10	4, 9
8	Св30	Лента светодиодная 24 В	на поверхности, профиль с рассеивателем, датчик движения	1,8 м	4,8/м	8,6	150/м	2700	90	—	20	нет	ночной	L11	4
9	Св38, Св39	Линейный светильник	на поверхности	1,2 м	8	16	700	3000	90	—	20	—	рабочий	L5	5
10	Св12–Св14, Св51	Встраиваемый точечный	в ГКЛ, корпус ≤ 70 мм	4	6	24	500	3000	90	—	44	—	общий	L12, L17	6, 11
11	Св15, Св52	Настенный светильник над зеркалом, драйвер встроен	над зеркалом, H=1900	2	8	16	600	3000	90	—	44	—	рабочий	L13, L18	6, 11
12	Св11, Св64, Св74	Настенный (бра)	на стене, H=1500	3	6	18	400	2700	90	60	20	—	рабочий	L19, L22	8, 10
13	Св65–Св72	Встраиваемый точечный	в ГКЛ, корпус ≤ 70 мм	8	12	96	1000	2700	90	—	20	—	общий	L20	10
14	Св73	Лента светодиодная 24 В	на поверхности, профиль с рассеивателем	15,5 м	9,6/м	148,8	900/м	2700	90	—	20	да	акцентный	L21	10
15	Св50	Встраиваемый точечный	в ГКЛ, корпус ≤ 70 мм	1	7	7	600	3000	90	—	44	—	общий	L17	11
		Итого		**54 шт + 48,5 м**		**1023,4**									

LED-ленты, линейные светильники и блоки питания

Марка	Пом.	L, м	U, В	Вт/м	Σ P, Вт	БП	P БП, Вт	Загр., %	Питание	Доступ к БП
Св23	1	12,3	24	9,6	118,1	БП2	200	59	с двух концов	люк 300×300 в коробе У1 у окна
Св10	3	5,4	24	9,6	51,8	БП1	100	52	с одного конца	люк 300×300 в коробе потолка у стены А
Св30	4	1,8	24	4,8	8,6	БП3	20	43	с одного конца	в шкафу M_11, верхняя полка
Св38	5	0,6	24	—	8	БП4	30	53	встроенный ввод	в колонне M_19 над холодильником, съёмная панель
Св39	5	0,6	24	—	8	БП4	30	53	встроенный ввод	в колонне M_19 над холодильником, съёмная панель
Св62	8	12,3	24	9,6	118,1	БП5	200	59	с двух концов	люк 300×300 в коробе У1 у окна
Св73	10	15,5	24	9,6	148,8	БП6	200	74	с двух концов	люк 300×300 в коробе У1 у входа


Сценарии (помещения со светорегуляторами)

Помещение	Сценарий	Горят группы (уровень)	Управление
3. Гостиная-столовая	Вечер	L2 подвес над обеденным столом — вкл.; L3 лента в карнизе (диммер) — 50 %; остальные выкл.	светорегулятор S2; выключатель S1
	Гости	L1 общий свет (споты) — вкл.; L2 подвес над обеденным столом — вкл.; L3 лента в карнизе (диммер) — 100 %	светорегулятор S2; выключатель S1
	Кино	L3 лента в карнизе (диммер) — 20 %; остальные выкл.	светорегулятор S2
	Уборка	L1 общий свет (споты) — вкл.; L2 подвес над обеденным столом — вкл.; остальные выкл.	выключатель S1

Примечания

1. Позиции и марки Св — те же, что на плане освещения (лист 39); группы L — по плану выключателей (лист 41).
2. Модели светильников не выбраны: лист — техническое задание на подбор. Модель по строке таблицы: поток, Тц, Ra, угол, IP и регулировка яркости не хуже указанных, мощность не больше; встраиваемые — под глубину короба (графа «Установка»). IP 20 — сухие помещения. После выбора моделей (артикул, производитель) лист выпускается как «Спецификация светильников».
3. Длина LED-ленты в карнизе — по линии карниза плана потолков (лист 32); Σ P = Вт/м × длина. Блок питания загружен не больше чем на 80 %; лента 24 В длиннее 10 м питается с двух концов; доступ к блоку питания — люк ревизии 300×300 мм или место, указанное в таблице.
4. Сценарии: % — яркость группы на светорегуляторе; «вкл.» — группа на обычной клавише; группы, не названные в строке, выключены. Светильники и блоки питания групп на светорегуляторе — с регулировкой яркости. Клавиши и светорегуляторы — лист 41.
5. В пом. 1, 8, 10 свет включается клавишами групп — лист 41.
6. Мощность и поток в таблице — требования к подбору (поток не меньше, мощность не больше указанных); после выбора модели — по её паспорту, Σ P — установленная мощность освещения. Оценка освещённости — на плане освещения; это не светотехнический расчёт.

					Проект: Квартира 103 м²
	Лист	№ док.	Подпись	Дата	
Дизайнер	Кырлан А.С.			04.11.26	Техническое задание на подбор светильников
					Стадия: П; Лист: 40; Листов: 96

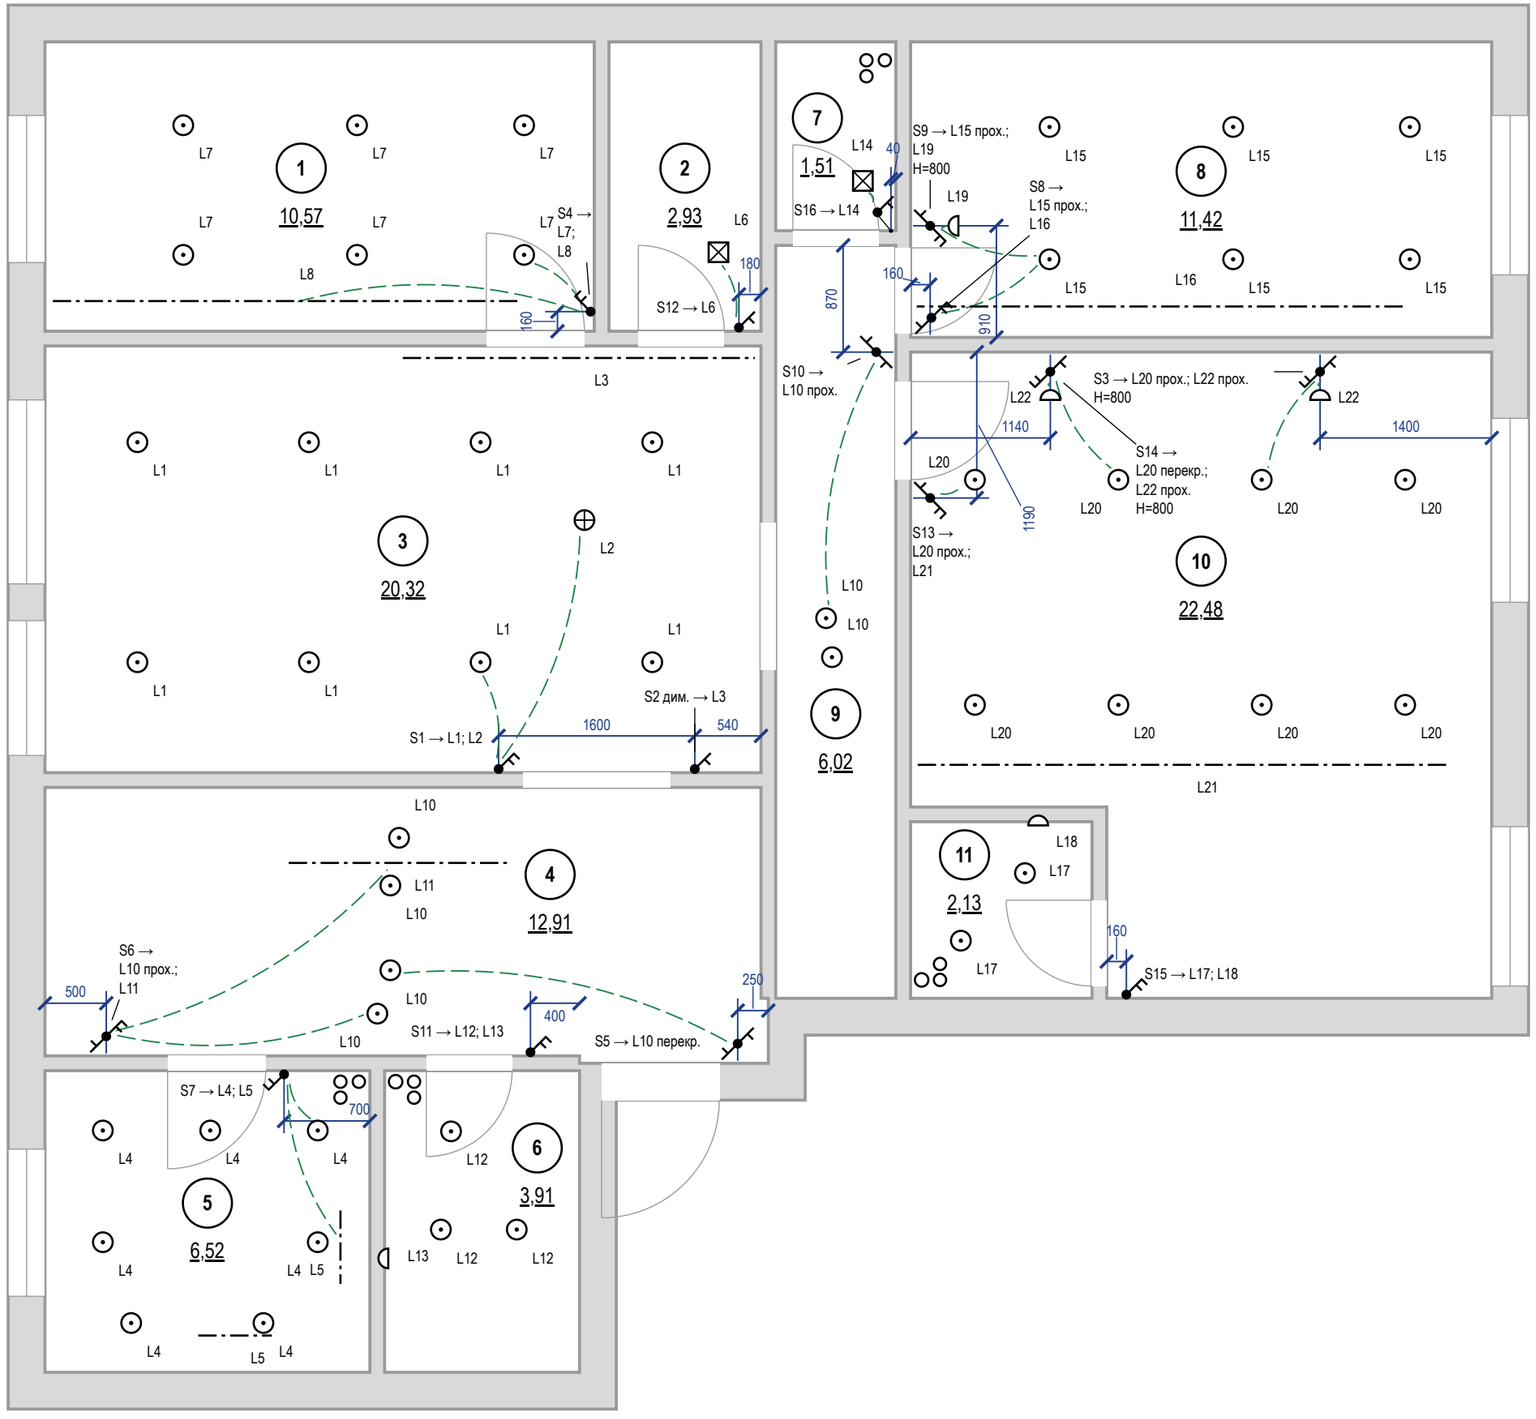


Условные обозначения

- выключатель одноклавишный
- выключатель двухклавишный (флажков — по числу клавиш)
- выключатель с проходной или перекрёстной клавишей (обратный флажок); тип клавиши — в подписи
- S1 → — марка → группы по клавишам (через «;»): прох. — проходной, перекр. — перекрёстный, дим. — светорегулятор; H — высота
- связь: выключатель → ближайший светильник группы в том же помещении (не трасса кабеля); полный состав группы — по номеру L
- светильник встраиваемый точечный
- светильник потолочный накладной
- светильник подвесной
- светильник настенный (бра), H — высота оси
- светодиодная лента в профиле / в карнизе короба
- L1 — группа включения у светильника
- стояк: К1 — канализация, В1 — ХВС, Т3 — ГВС
- 1 — номер помещения, площадь м²

Примечания

1. За отметку 0,000 принят уровень чистого пола. Высоты H — от чистого пола до оси изделия; привязки — от чистовой грани стены до оси механизма (у рамки на несколько постов — до оси рамки).
2. Высота установки, не указанная на плане: выключатели — 900 мм от чистого пола (у кровати и другие — H у марки), со стороны дверной ручки (ПУЭ 7.1.51).
3. Какой выключатель какие светильники включает — по номеру группы L: у выключателя (S1 → L1; L2 — клавиши по порядку) и у каждого светильника. Пунктир — подсказка к ближайшему светильнику группы в том же помещении (не дальше 3 м), это не трасса кабеля; выключатель за стеной (у двери санузла) и далёкая группа только номер группы.
4. Группы из нескольких мест (L10 — S5, S6, S10; L15 — S8, S9; L20 — S3, S13, S14; L22 — S3, S14): на крайних местах — проходные клавиши, на промежуточных — перекрёстные; механизмы — в ведомости изделий.
5. Светорегулятор — по заднему фронту (для LED-драйверов), совместимость с драйверами проверить до закупки.
6. Розеточные и мокрые линии — через УЗО или дифавтомат с током утечки не более 30 мА (ПУЭ 7.1.79); в санузле выполнить ДСУП (ПУЭ 7.1.87–7.1.88).
7. Кабель — медный, исполнение нг(А)-LS (ГОСТ 31565-2012); скрытая прокладка только горизонтально и вертикально, фактические трассы зафиксировать исполнительной схемой до закрытия отделки.
8. Расчёт нагрузок, токов КЗ, селективности и сечений — по проекту ЭОМ организации с допуском СРО; лист задаёт состав, расположение и группы.

					Проект: Квартира 103 м²	М 1:50
	Лист	№ док.	Подпись	Дата	Управление светильниками	Стадия / Лист / Листов
Дизайнер	Кырлан А.С.			04.11.26		П / 41 / 96

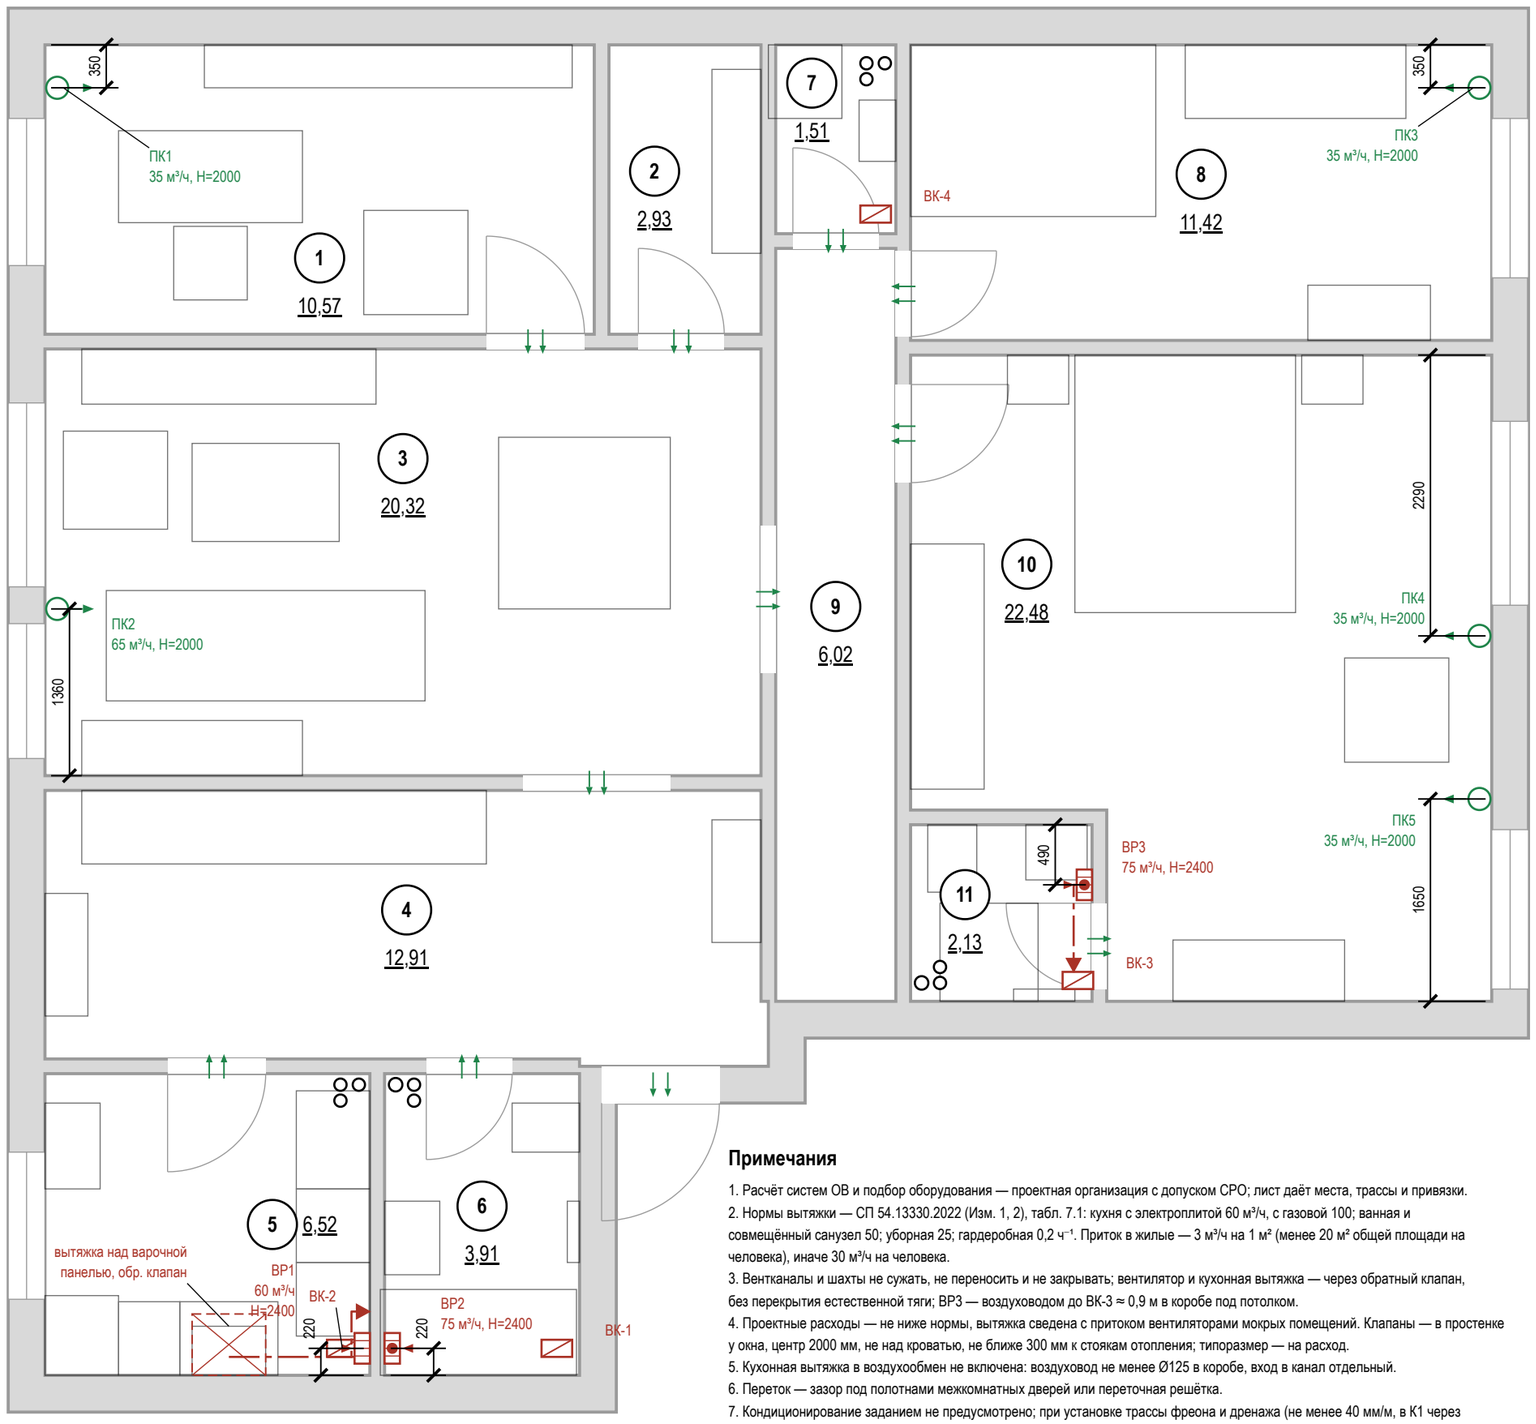

Условные обозначения

- стояк: К1 — канализация, В1 — ХВС, Т3 — ГВС
- номер помещения, площадь м²
- вытяжная решётка в вентканал: марка, расход м³/ч, Н центра от чистого пола
- вытяжная решётка с бытовым вентилятором и обратным клапаном: марка, расход, Н
- приточный клапан (КИВ) в наружной стене: марка, расход, Н центра
- переток: зазор под полотном или переточная решётка
- кухонная вытяжка над варочной панелью
- вентканал ВК-N в стене или вентблоке
- воздуховод в коробе под потолком (за подшивным потолком) до вентканала
- отдельный вход воздуховода в вентканал, обратный клапан

Воздухообмен, м³/ч

№	Помещение	Выт. норма	Выт. проект	Прит. норма	Прит. проект	Устрой-ства
1	Кабинет-библиотека			32	35	ПК1
2	Кладовая	2				переток
3	Гостиная-столовая			61	65	ПК2
5	Кухня	60	60			ВР1
6	Ванная	50	75			ВР2
7	Постирочная	1				переток
8	Спальня 2			35	35	ПК3
10	Спальня мастер			68	70	ПК4, ПК5
11	Ванная мастер	50	75			ВР3
	Итого	**163**	**210**	**196**	**205**	
	Норма по жильцам: 30×2			60		

Воздухообмен квартиры — по большей из сумм притока и вытяжки: норма 196 м³/ч, проект 210 м³/ч.
Вытяжка не меньше притока — баланс сведён.

Примечания


1. Расчёт систем ОВ и подбор оборудования — проектная организация с допуском СРО; лист даёт места, трассы и привязки.
2. Нормы вытяжки — СП 54.13330.2022 (Изм. 1, 2), табл. 7.1: кухня с электроплитой 60 м³/ч, с газовой 100; ванная и совмещённый санузел 50; уборная 25; гардеробная 0,2 ч⁻¹. Приток в жилые — 3 м³/ч на 1 м² (менее 20 м² общей площади на человека), иначе 30 м³/ч на человека.
3. Вентканалы и шахты не сужать, не переносить и не закрывать; вентилятор и кухонная вытяжка — через обратный клапан, без перекрытия естественной тяги; ВР3 — воздуховодом до ВК-3 ≈ 0,9 м в коробе под потолком.
4. Проектные расходы — не ниже нормы, вытяжка сведена с притоком вентиляторами мокрых помещений. Клапаны — в простенке у окна, центр 2000 мм, не над кроватью, не ближе 300 мм к стоякам отопления; типоразмер — на расход.
5. Кухонная вытяжка в воздухообмен не включена: воздуховод не менее Ø125 в коробе, вход в канал отдельный.
6. Переток — зазор под полотнами межкомнатных дверей или переточная решётка.
7. Кондиционирование заданием не предусмотрено; при установке трассы фреона и дренажа (не менее 40 мм/м, в К1 через сифон) и питание заложить до черновых работ.
8. Привязки оборудования — по паспортам приобретённых моделей, до черновых работ.

	Лист	№ док.	Подпись	Дата
Дизайнер	Кырлан А.С.			04.11.26

Проект: Квартира 103 м² — **М 1:50**

План вентиляции

Стадия	Лист	Листов
П	42	96

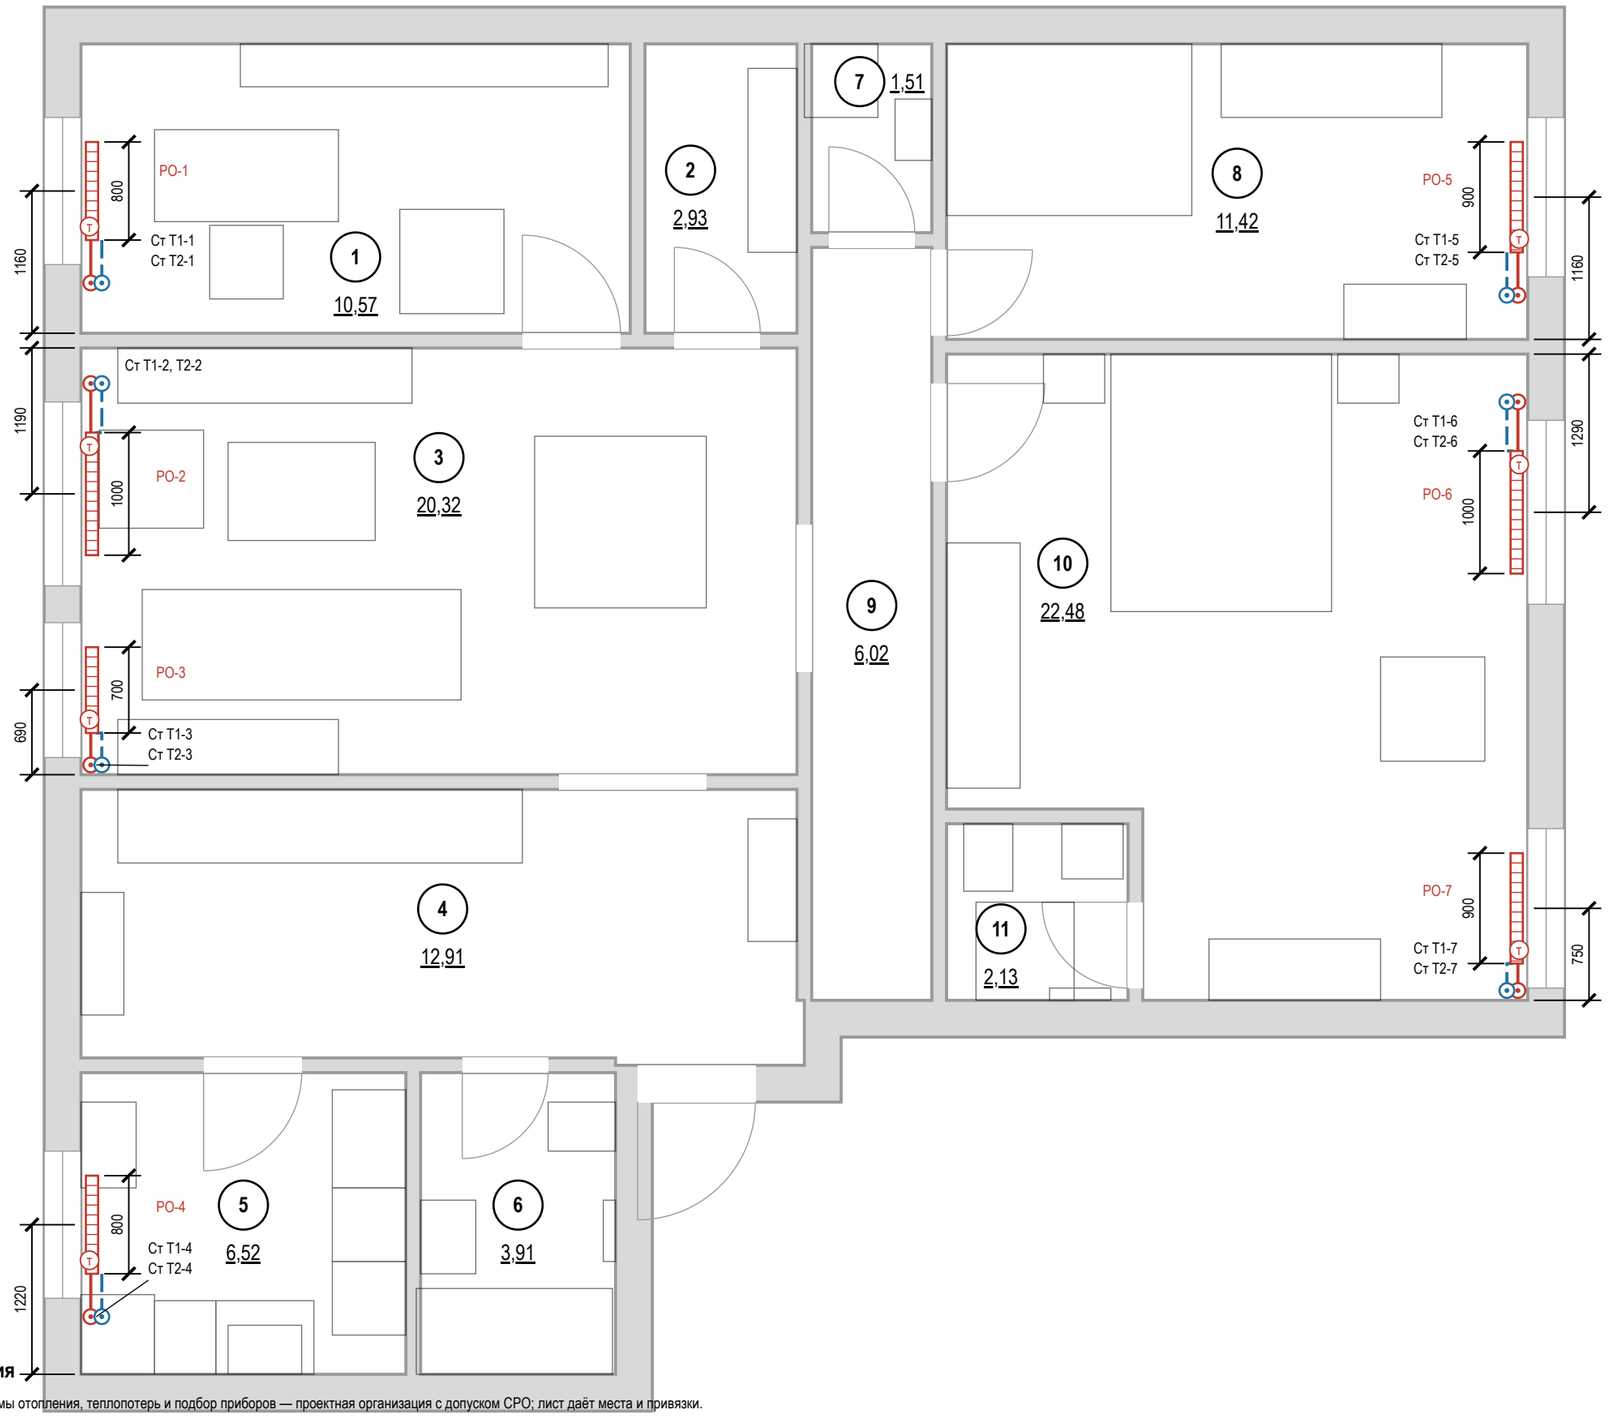

Условные обозначения

- (1) — номер помещения, площадь м²
- радиатор отопления (марка РО-N, длина по плану)
- (Т) — клапан с термоголовкой на подаче
- стояк отопления, подающий (Ст Т1-N)
- стояк отопления, обратный (Ст Т2-N)
- Т1 — отопление, подающий трубопровод
- Т2 — отопление, обратный трубопровод

Ведомость радиаторов

Марка	Помещение	Тип	Д×В×Г, мм	Низ / стена	Q, Вт
РО-1	1. Кабинет-библиотека	панельный	800×400×100	120 / 40	расч.
РО-2	3. Гостиная-столовая	панельный	1000×400×100	120 / 40	расч.
РО-3	3. Гостиная-столовая	панельный	700×400×100	120 / 40	расч.
РО-4	5. Кухня	панельный	800×500×100	120 / 40	расч.
РО-5	8. Спальня 2	панельный	900×500×100	120 / 40	расч.
РО-6	10. Спальня мастер	панельный	1000×500×100	120 / 40	расч.
РО-7	10. Спальня мастер	панельный	900×500×100	120 / 40	расч.

тип и мощность — по теплотехническому расчёту
Низ — от чистого пола, стена — зазор до задней панели, мм.

Привязки — до обмера
Стояки отопления в исходных данных не заданы: показаны у откосов окон, подводки — принципиально. До черновых работ — обмер стояков и паспорта приборов; лист перевыпустить по факту.

Примечания

1. Расчёт системы отопления, теплопотерь и подбор приборов — проектная организация с допуском СРО; лист даёт места и привязки.
2. Тип, длина и мощность радиаторов — по теплотехническому расчёту; лист задаёт места, зазоры и подключение.
3. Радиаторы — под каждым окном жилых комнат и кухни, центр по оси проёма, длина 0,7 ширины окна (кратно 100); окончательно — по расчёту.
4. Зазоры радиатора: низ не менее 100 мм от чистого пола, верх не менее 100 мм до подоконника, 30–50 мм от стены до задней панели; центр по оси окна с допуском ±20 мм. Верх до подоконника — 215 мм (РО-1 — 200, РО-4 — 143, РО-5 — 163, РО-6 — 205, РО-7 — 205).
5. Радиаторы не закрывать глухими коробами и мебелью; перенос и замена приборов в многоквартирном доме — переустройство, согласование с управляющей организацией (ЖК РФ ст. 25–26); вынос на лоджию запрещён.
6. Трубы отопления через межквартирные стены не прокладывать (СП 51.13330.2011, п. 9.19); через перекрытия и перегородки — в гильзах.
7. Привязки приборов и подводок — по паспортам приобретённых радиаторов и клапанов, до черновых работ.
8. До закрытия отделкой трубопроводы отопления испытать гидростатическим давлением с оформлением акта (СП 73.13330.2016, 7.2–7.3).

	Лист	№ док.	Подпись	Дата
Дизайнер	Кырлан А.С.			04.11.26

Проект: Квартира 103 м² — **М 1:50**

План отопления


Стадия	Лист	Листов
П	43	96

Спецификация плинтусов

Наименование	Помещения	Длина, м (с запасом)
Ultrawood Base 5340, ЛДФ под окраску, 83×15 мм, 2440 мм (арт. LDF-BASE-5340), крепление к стене, окраска в цвет Farrow & Ball No. 291	1, 3, 4, 5, 8, 9, 10	102
Ultrawood Base 5340, ЛДФ под окраску, 83×15 мм, 2440 мм (арт. LDF-BASE-5340), крепление к стене, окраска в цвет NCS S 0502-Y	2, 7	12

Отметки по высоте






±0,000	чистый пол пом. 1–5, 7–10; отсчёт высот
−0,015	чистый пол пом. 6, 11, ниже на 15 мм
−0,064	верх плиты — расчёт, не замер (задание на обмер)
сущ. пол	снимается до плиты; не замерен (задание на обмер)

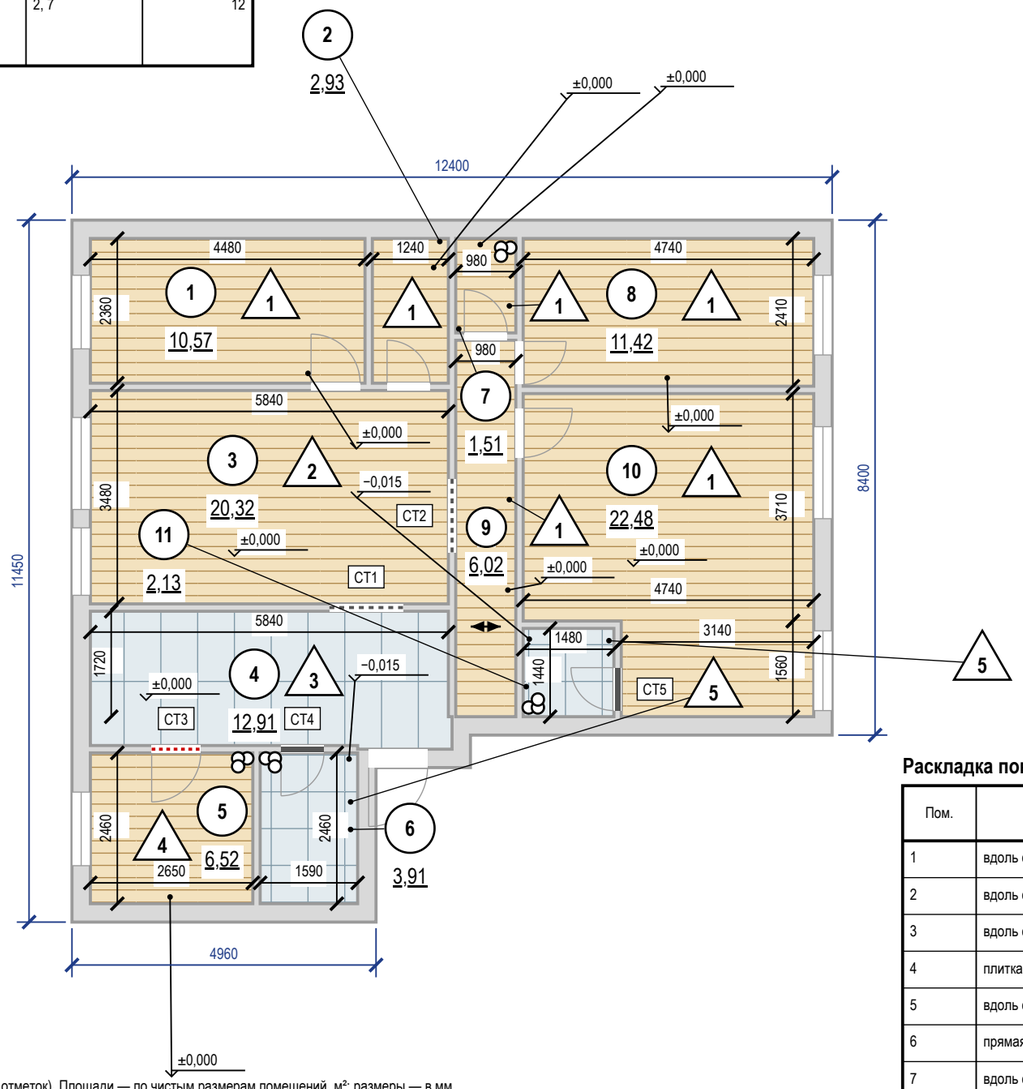

Примечания

1. За отметку ±0,000 принят чистый пол, не существующий (блок отметок). Площади — по чистым размерам помещений, м²; размеры — в мм.
2. Стык разнотипных покрытий — по оси дверного полотна (под полотном в закрытом положении); решение стыка — по ведомости стыков.
3. Размеры помещений в свету (ширина × длина, мм), не поместившиеся на плане: пом. 2 — 1240 × 2360; пом. 4 — 5840 × 1720, 5900 × 470, 1540 × 60; пом. 7 — 980 × 1540; пом. 9 — 980 × 6140.
4. Пол санузлов ниже смежных помещений на 15 мм за счёт меньшей толщины стяжки (верх плиты общий — по экспликации полов); гидроизоляция по стяжке с заведением на стены не менее 200 мм (СП 29.13330.2011, п. 7.2), до облицовки — тест проливом и акт скрытых работ.
5. Трубопроводы в конструкции пола не прокладываются: пирог пола 49–64 мм не вмещает выпуски канализации с уклоном — выпуски К1 ведутся по стенам над чистым полом в коробах (лист 19).
6. Звукоизоляционный слой под стяжкой проектом не предусмотрен (стяжка по плите): приведённый уровень ударного шума перекрытия с полом Lnw не более 60 дБ (СП 51.13330.2011, табл. 2) подтвердить по данным дома; при превышении — плавающая стяжка по звукоизоляции с демпферной лентой по контуру и у стояков, пирог пересчитать.
7. Штучные покрытия (инженерная доска): направление — по стрелке; влажность основания по СМ не более 2,0 % (по ТУ изготовителя).
8. Ровность основания — просвет под 2-метровой рейкой не более 2 мм: пом. 1, 2, 3, 5, 7, 8, 9, 10 (инженерная доска), пом. 4, 6, 11 (керамогранит); проверить до укладки покрытия (СП 71.13330.2017, табл. 8.5).
9. Сетка на плитке — условная, в размер формата; точка старта и раскладка — по листу раскладки плитки.
10. Узор покрытия (заливка-код типа пола) прерывается под надписями — площадями помещений и отметками чистого пола.
11. Пироги полов — по экспликации полов: слои сверху вниз, толщины в мм; гидроизоляция мокрых зон — в пироге и в ведомости отделки; схема пола — без масштаба.

Экспликация полов

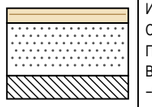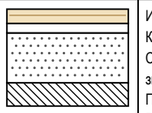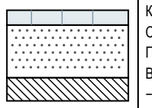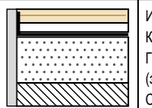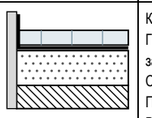Номер помещения	Тип пола	Схема пола	Данные элементов пола (наименование, толщина, основание), мм	Площадь, м²
1, 2, 7, 8, 9, 10	1		Инженерная доска на клею — 14 Стяжка ЦПС М200 — 50 Плита перекрытия Всего 64 мм; ЧП ±0,000, верх плиты −0,064	54,93
3	2		Инженерная доска дуб на клею — 14 Клей паркетный МС-полимерный — 1 Стяжка ЦПС М300 (В22,5), фибра, по звукоизоляции — 49 Плита перекрытия монолитная Всего 64 мм; ЧП ±0,000, верх плиты −0,064	20,32
4	3		Керамогранит на клею C2 TE S1 — 14 Стяжка ЦПС М200 — 50 Плита перекрытия Всего 64 мм; ЧП ±0,000, верх плиты −0,064	12,91
5	4		Инженерная доска дуб на клею — 14 Клей паркетный МС-полимерный — 1 Гидроизоляция полиуретановая, 2 слоя (зона мойки и острова) — 2 Стяжка ЦПС М300 (В22,5), фибра, по звукоизоляции — 47 Плита перекрытия монолитная Всего 64 мм; ЧП ±0,000, верх плиты −0,064	6,52
6, 11	5		Керамогранит на клею C2 TE S1 — 14 Гидроизоляция обмазочная, 2 слоя, с заведением на стены 200 мм — 2 Стяжка ЦПС М200 — 33 Плита перекрытия Всего 49 мм; ЧП −0,015, верх плиты −0,064	6,04
			Итого	**100,72**

Раскладка покрытий

Пом.	Укладка	Старт (оси от чистовых стен), мм	Отступ 1-го ряда / крайние плитки, мм
1	вдоль стен A/B, прямая	от стены A, 1-й ряд вдоль неё	зазор от стены не задан
2	вдоль стен A/B, прямая	от стены A, 1-й ряд вдоль неё	зазор от стены не задан
3	вдоль стен A/B, прямая	от стены A, 1-й ряд вдоль неё	зазор от стены не задан
4	плитка	раскладка плиточника не задана	
5	вдоль стен A/B, прямая	от стены A, 1-й ряд вдоль неё	зазор от стены не задан
6	прямая, сетка 600×600, шов 2	ось X 771 от Г; ось Y 1206 от A	X 469 / 469; Y 302 / 302
7	вдоль стен A/B, прямая	от стены A, 1-й ряд вдоль неё	зазор от стены не задан
8	вдоль стен A/B, прямая	от стены A, 1-й ряд вдоль неё	зазор от стены не задан
9	вдоль стен A/B, прямая	от стены A, 1-й ряд вдоль неё	зазор от стены не задан
10	вдоль стен A/B, прямая	от стены A, 1-й ряд вдоль неё	зазор от стены не задан
11	прямая, сетка 600×600, шов 2	ось X 716 от Г; ось Y 696 от A	X 414 / 414; Y 394 / 394


	Лист	№ док.	Подпись	Дата
Дизайнер	Кырлан А.С.			04.11.26

Проект: Квартира 103 м² — **М 1:100**


План покрытий пола

Стадия	Лист	Листов
П	44	96

Фрагмент 1. Ванная (пом. 6). Пол 600×600, шов 2 мм, М 1:25

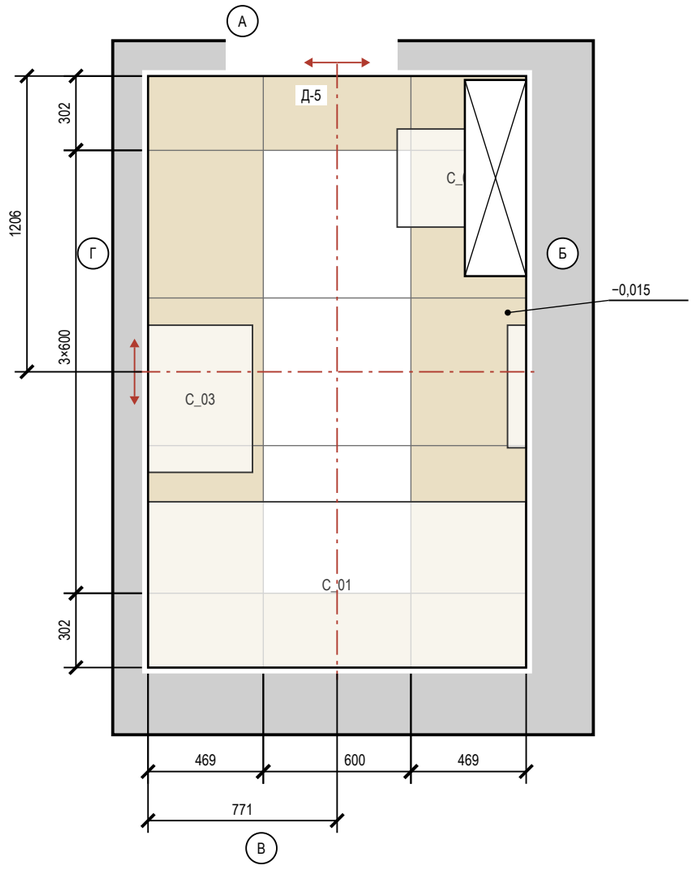

Фрагмент 2. Ванная мастер (пом. 11). Пол 600×600, шов 2 мм, М 1:25

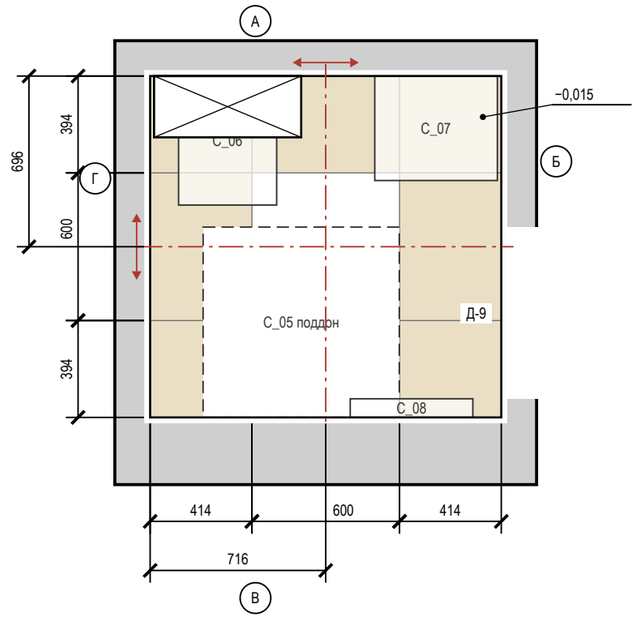

Ведомость материалов

Материал	Класс, код	Норма расхода	Кол-во
Затирка	CG2WA Mapei Ultracolor Plus 132	(a+b)/ab·шов·t·1,6	3,0 кг
Затирка	CG2WA	(a+b)/ab·шов·t·1,6	1,0 кг
Клей	C2 TE S1 Ceresit CM 17	1,5 кг/м²·мм, слой 5	297 кг (12 меш.)
Клей	C2 TE S1	1,5 кг/м²·мм, слой 5	105 кг (5 меш.)
Гидроизоляция	обмазочная, 2 слоя: пол, стены по периметру и зоны замачивания	по ТУ	18,7 м²
Демпф. лента	по периметру пола из плитки		27,1 м

Ведомость плитки

Помещение, поверхность	Плитка, код	Формат	Шов	S, м²	Целых	Подр.	С запасом
Ванная, пол	Atlas Concorde Marvel Travertine Sand Cross 60×60 Matte Sensitech, арт. AFUL (той же коллекции, что стены A8UZ; тон сверить по образцу)	600×600	2	3,91	3	12	17
Ванная, стены А–Г	A8UZ	600×1200	2	17,04	13	19	36
Ванная, короб инсталляции	A8UZ	600×1200	2	1,76	0	6	7
Ванная мастер, пол	Atlas Concorde Marvel Travertine Sand Cross 60×60 Matte Sensitech, арт. AFUL (той же коллекции, что стены A8UZ; тон сверить по образцу)	600×600	2	2,13	0	8	9
Ванная мастер, стены А–Г	A8UZ	600×1200	2	11,85	5	19	28
Ванная мастер, короб инсталляции	A8UZ	600×1200	2	1,47	1	3	5
Прихожая-холл, пол	A8UZ	600×1200	2	12,91	0	20	22
Итого 600×600				6,04	3	20	26
Итого 600×1200				**45,03**	**19**	**67**	**98**

Условные обозначения


- плитка целая; тонкая линия — шов
- плитка с подрезкой (размер — на цепочке)
- ось старта; стрелки — направление укладки
- сантехприбор: габарит, высота по практике
- поддон душа — плитку пола под ним не кладут
- короб инсталляции: плитка пола — до короба
- отметка чистого пола на полке выноски, м
- (А) обозначение стены А–Г (как на развёртках)

Примечания

1. Раскладка от чистовых размеров: стены санузлов теряют 10 + 5 + 9 = 24 мм на сторону (штукатурка, клей, плитка); подрезки — чистые, без шва.
2. Старт — от центра помещения (штрихпунктир, стрелки — направление укладки); размер старта — от чистовых стен Г и А.
3. Раскладка пола «Прихожая-холл» — на листе «Раскладка плитки. Прихожая-холл».
4. Калибр партии не задан — до укладки замерить (рабочий размер W, ГОСТ 13996-2019) и пересчитать подрезки.
5. Количество: целые по раскладке + по одной на подрезку, запас 10 %; один артикул — одна партия и тон. Исключены поддон, короб, проёмы и места за коробом; S — по чистым граням: стены нетто = зона облицовки по ведомости отделки − место за коробом инсталляции 1,68 м² (плитку за коробом не кладут), короб — отдельной строкой.
6. Клей C2 TE S1 Ceresit CM 17; C2 TE S1 (ГОСТ Р 56387-2018), затирка CG2WA Mapei Ultracolor Plus 132; CG2WA; расход — по ТУ выбранной марки.
7. Гидроизоляция: пол и стены 200 мм от ЧП; над ванной — до 2000 и 300 мм за борт (пом. 6), у душа — до 2000 и 500 мм за поддон (пом. 11) (см. развёртки); акт скрытых работ, пролив 24 ч.
8. Швы пола совмещены со швами стены А; по периметру — демпферная лента.
9. Отметка чистого пола −0,015, порог 15 мм; стык с соседним покрытием — по оси полотна двери.

					Проект: Квартира 103 м²		**М 1:25**
	Лист	№ док.	Подпись	Дата	Раскладка плитки. Планы полов	Стадия	Лист	Листов
Дизайнер	Кырлан А.С.			04.11.26		П	45	96

Фрагмент 1. Прихожая-холл (пом. 4). Пол 600×1200, шов 2 мм, М 1:20

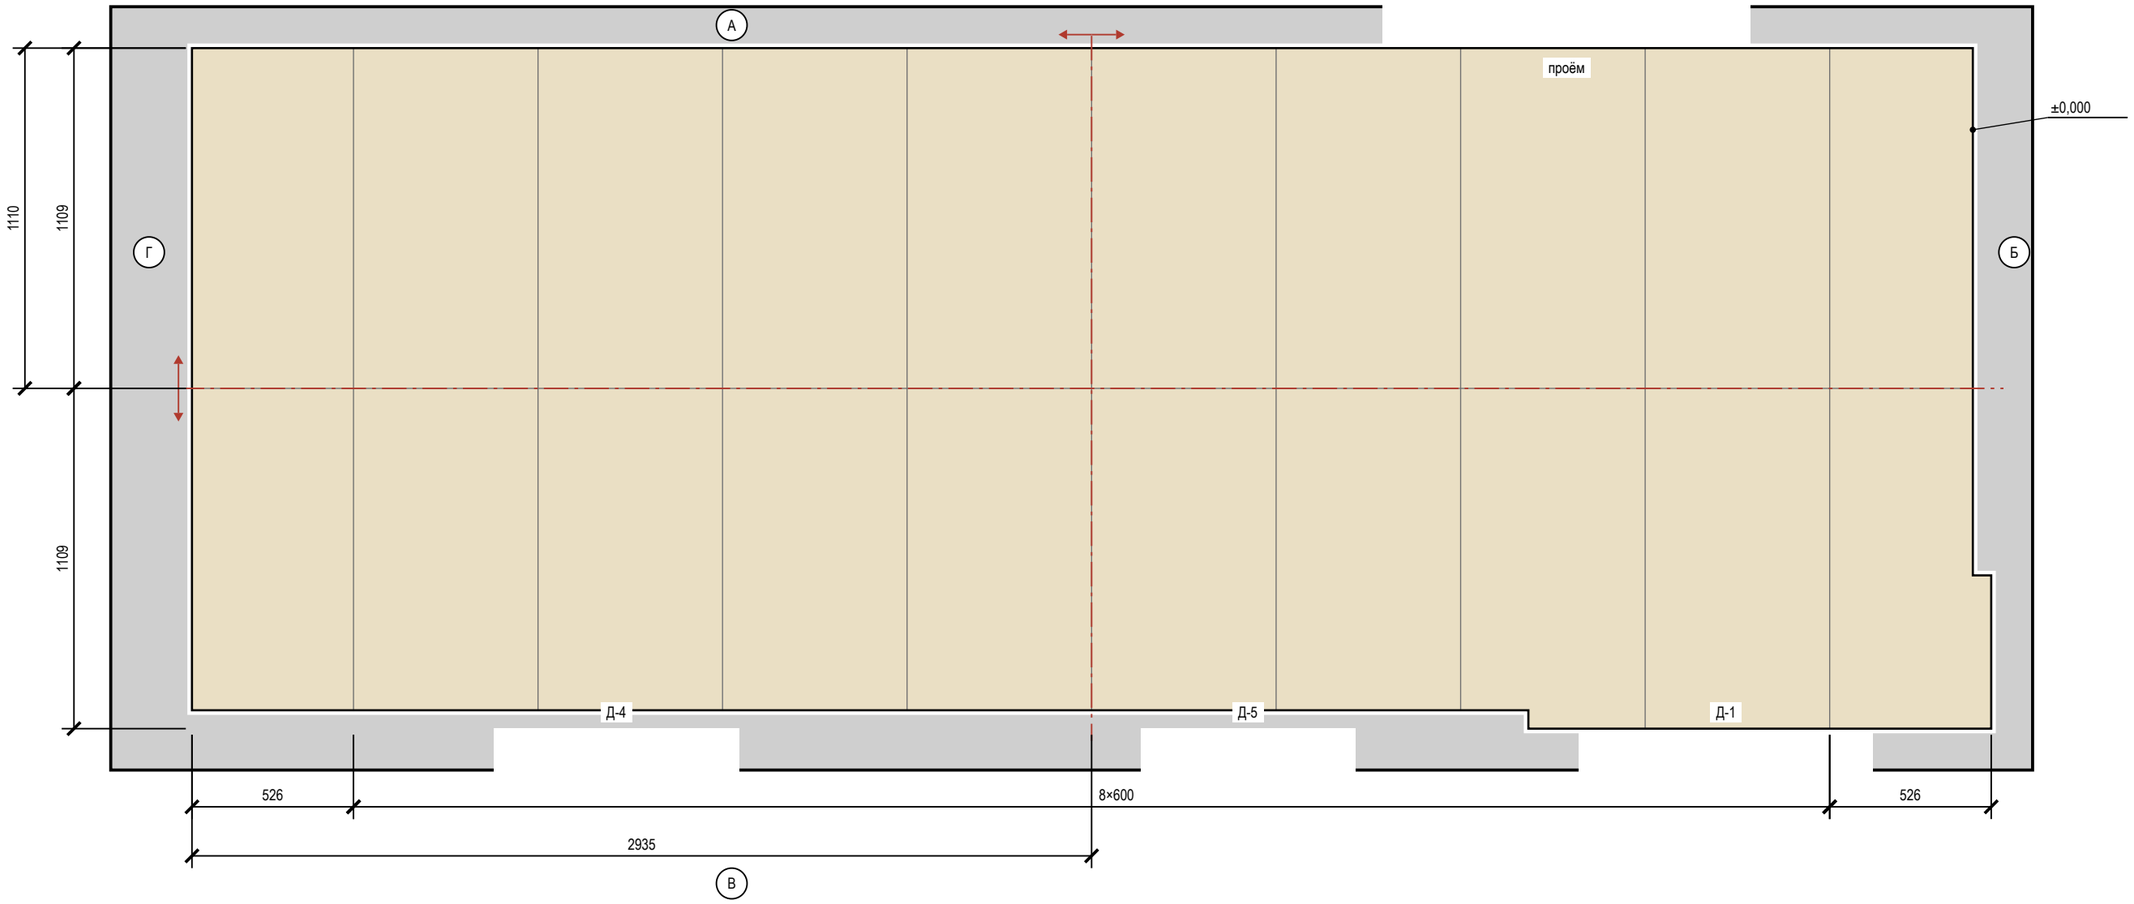

Условные обозначения

- плитка целая; тонкая линия — шов
- плитка с подрезкой (размер — на цепочке)
- ось старта; стрелки — направление укладки
- отметка чистого пола на полке выноски, м
- (А) обозначение стены А–Г (как на развёртках)

Подсчёт плитки

Поверхность	Формат	S, м²	Целых	Подр.	С запасом
Прихожая-холл, пол	600×1200	12,91	0	20	22

Примечания

1. Прихожая-холл: керамогранит 600×1200, длинная сторона — вдоль стен Б и Г, шов 2 мм, прямая раскладка от центра. Стены окрашены: раскладка от чистового контура минус штукатурка и шпаклёвка 15 мм на сторону (принято); подрезки 526 / 1109 мм, срез — под плинтус.
2. Прихожая-холл: деформационный зазор по периметру 8–10 мм под плинтусом; в проёмах — стык с соседним покрытием по оси полотна двери. Клей C2 TE S1, затирка CG2WA.
3. Клей, затирка и итог по форматам — в ведомостях листа «Раскладка плитки. Планы полов».

					Проект: Квартира 103 м² — **М 1:20**
	Лист	№ док.	Подпись	Дата	Раскладка плитки. Прихожая-холл
Дизайнер	Кырлан А.С.			04.11.26	Стадия: П; Лист: 46; Листов: 96

выпуск 04.11.2026 № d6a6e5e88d · стр. 46 из 96

Развёртка стены А


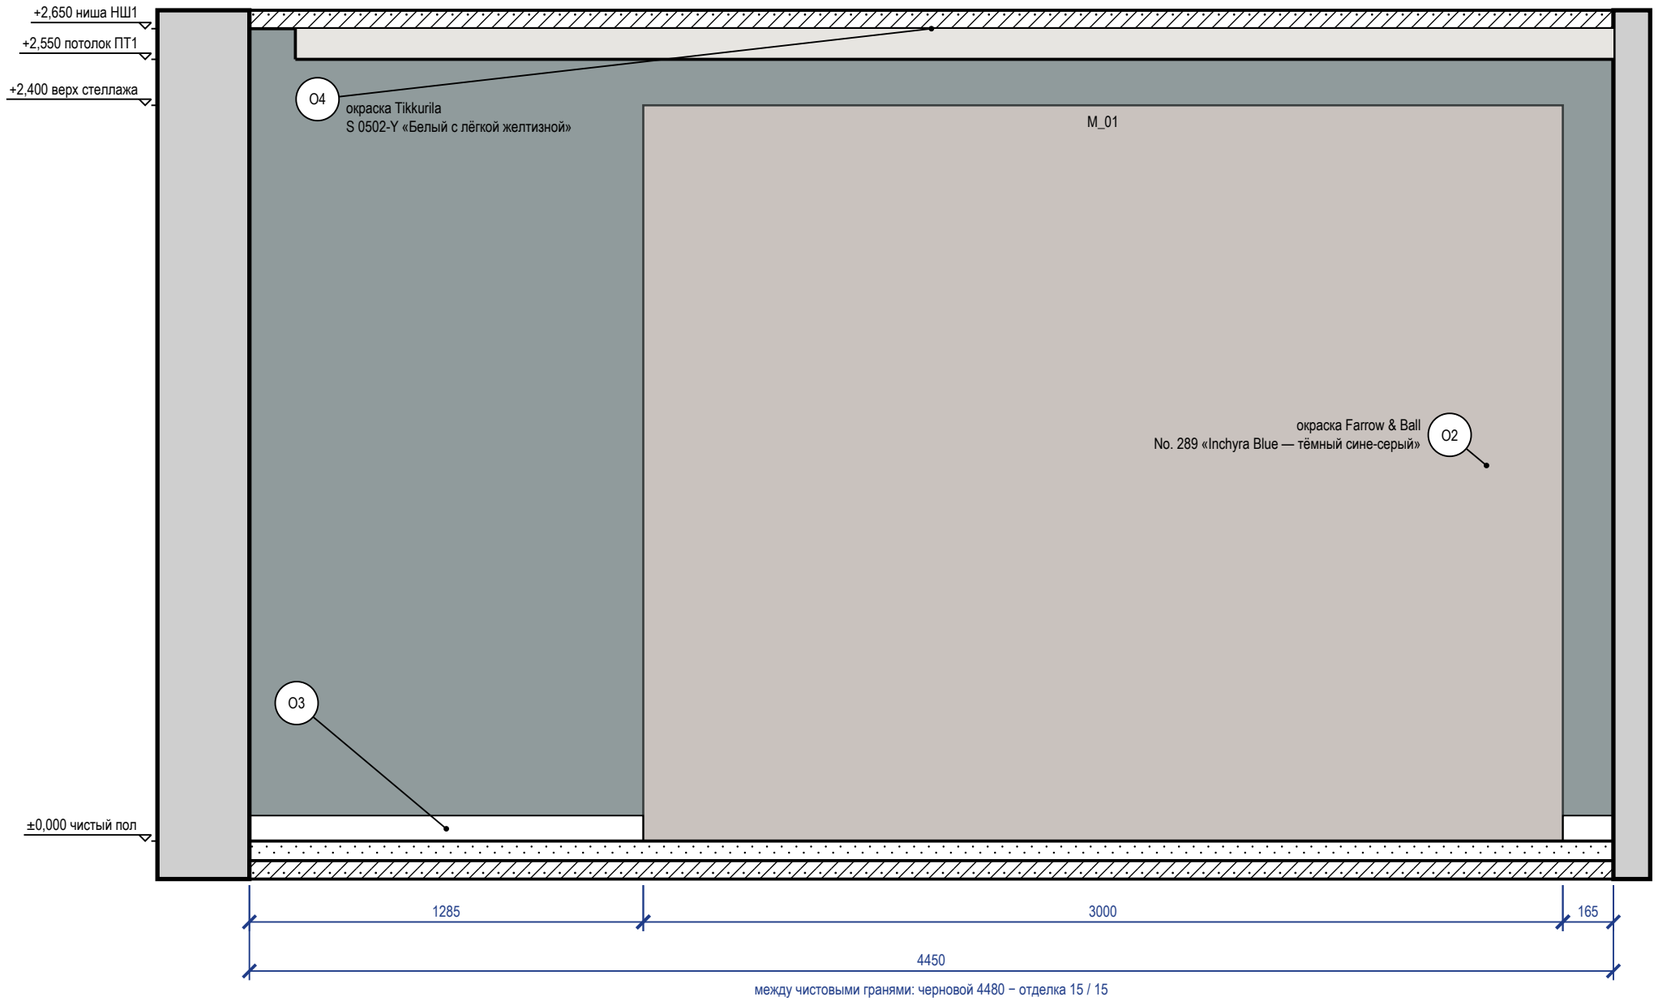


Схема развёрток (М 1:100)

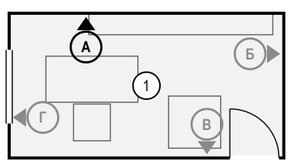

Ведомость отделки (на листе)


Марка	Поверхность	Материал, изделие	Цвет, код	Кол.
O2	акцентная стена	окраска, Farrow & Ball Modern Emulsion, матовая, подготовка Q3	Farrow & Ball No. 289 «Inchyra Blue — тёмный сине-серый»	11,8 м²
O3	плинтус	плинтус МДФ, h 83 мм, Ultrawood Base 5340, ЛДФ под окраску, 83×15 мм, 2440 мм (арт. LDF-BASE-5340)	Farrow & Ball No. 291 «School House White тёплый меловой белый»	1,4 м
O4	потолок	окраска, Tikkurila Anti-Reflex 2, глубокоматовая, подготовка Q3	NCS S 0502-Y «Белый с лёгкой желтизной»	10,6 м²

Примечания

1. Размеры — в мм от чистовых поверхностей стен; условные обозначения и общие указания — лист 3.


					Проект: Квартира 103 м²	М 1:20
	Лист	№ док.	Подпись	Дата		
Дизайнер	Кырлан А.С.			04.11.26	Развёртка стены А. Кабинет-библиотека (пом. 1)	Стадия: П; Лист: 47; Листов: 96

Развёртка стены Б

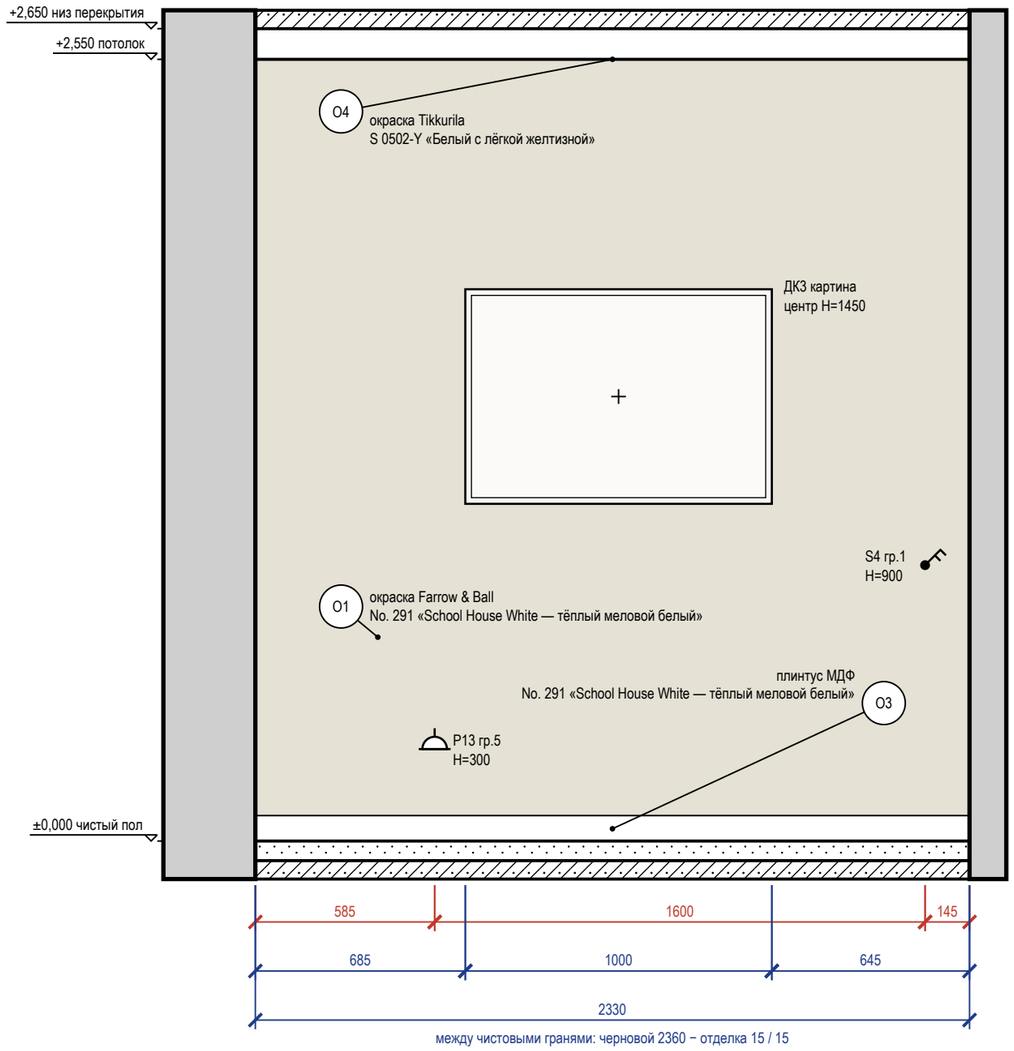


между чистовыми гранями: черновой 2360 − отделка 15 / 15

Развёртка стены Г

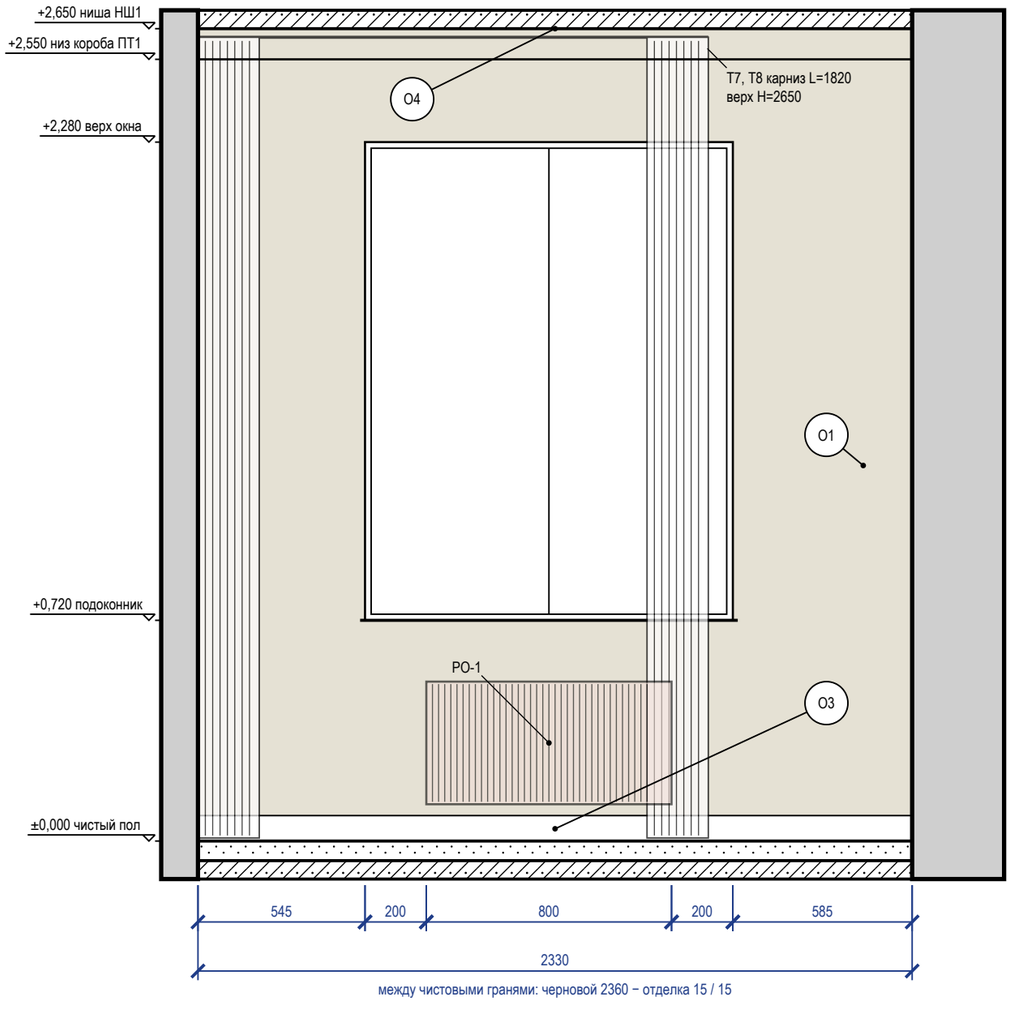

между чистовыми гранями: черновой 2360 − отделка 15 / 15

Схема развёрток (М 1:100)

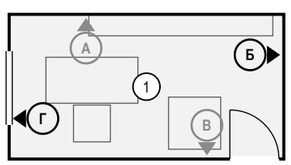

Ведомость отделки (на листе)

Марка	Поверхность	Материал, изделие	Цвет, код	Кол.
О1	стены	окраска, Farrow & Ball Modern Emulsion, матовая, подготовка Q3	Farrow & Ball No. 291 «School House White тёплый меловой белый»	10,2 м²
О3	плинтус	плинтус МДФ, h 83 мм, Ultrawood Base 5340, ЛДФ под окраску, 83×15 мм, 2440 мм (арт. LDF-BASE-5340)	Farrow & Ball No. 291 «School House White тёплый меловой белый»	4,7 м
О4	потолок	окраска, Tikkurila Anti-Reflex 2, глубокоматовая, подготовка Q3	NCS S 0502-Y «Белый с лёгкой желтизной»	10,6 м²

Примечания

1. Размеры — в мм от чистовых поверхностей стен; условные обозначения и общие указания — лист 3.
2. Картины и зеркала крепить к основанию по паспорту изделия (закладные и анкеры — в перечне скрытых работ); крест — ось центра предмета.
3. Карнизы (шины) — по ведомости текстиля декоратора: длина L и верх H на развёртке — те же числа, что в ведомости; крепление — до окраски потолка.
4. Карниз Т7, Т8: по ведомости текстиля шина L=1820 мм, а от её начала до чистового угла стены — 1665 мм: шина не встаёт, длину согласовать с декоратором до заказа.
5. Линии узора (швы плитки, складки штор, рёбра радиаторов) прерываются у знаков и выносок — просвет между линиями не менее 0,7 мм.

					Проект: Квартира 103 м²	М 1:20
	Лист	№ док.	Подпись	Дата		
Дизайнер	Кырлан А.С.			04.11.26	Развёртки стен Б, Г. Кабинет-библиотека (пом. 1)	Стадия: П; Лист: 48; Листов: 96

Развёртка стены В


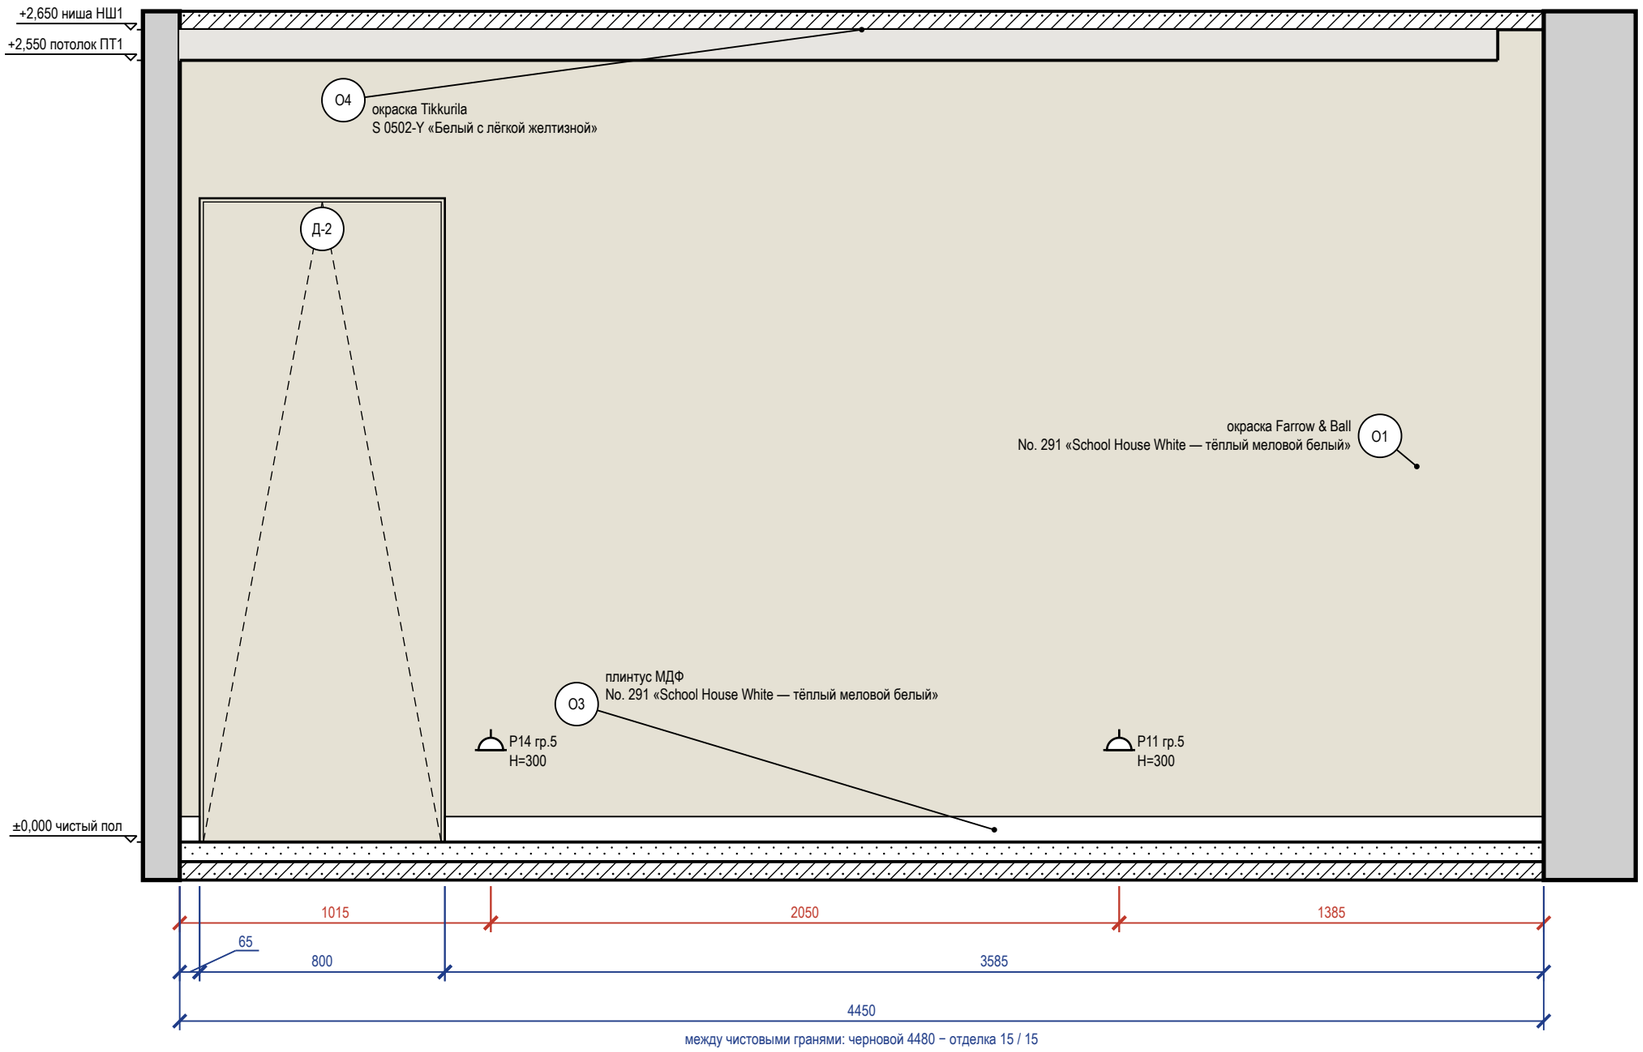


Схема развёрток (М 1:100)

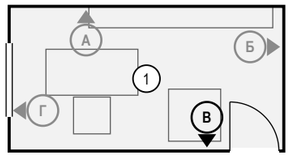

Ведомость отделки (на листе)

Марка	Поверхность	Материал, изделие	Цвет, код	Кол.
О1	стены	окраска, Farrow & Ball Modern Emulsion, матовая, подготовка Q3	Farrow & Ball No. 291 «School House White тёплый меловой белый»	10,1 м²
О3	плинтус	плинтус МДФ, h 83 мм, Ultrawood Base 5340, ЛДФ под окраску, 83×15 мм, 2440 мм (арт. LDF-BASE-5340)	Farrow & Ball No. 291 «School House White тёплый меловой белый»	3,6 м
О4	потолок	окраска, Tikkurila Anti-Reflex 2, глубокоматовая, подготовка Q3	NCS S 0502-Y «Белый с лёгкой желтизной»	10,6 м²


Примечания

1. Размеры — в мм от чистовых поверхностей стен; условные обозначения и общие указания — лист 3.
2. Двери скрытого монтажа — полотно в плоскости стены, отделка стены по полотну, плинтус прерывается у короба (узел — на листе узлов).

					Проект: Квартира 103 м² — М 1:20
	Лист	№ док.	Подпись	Дата	Развёртка стены В. Кабинет-библиотека (пом. 1)
Дизайнер	Кырлан А.С.			04.11.26	

Стадия	Лист	Листов
П	49	96

Развёртка стены Б

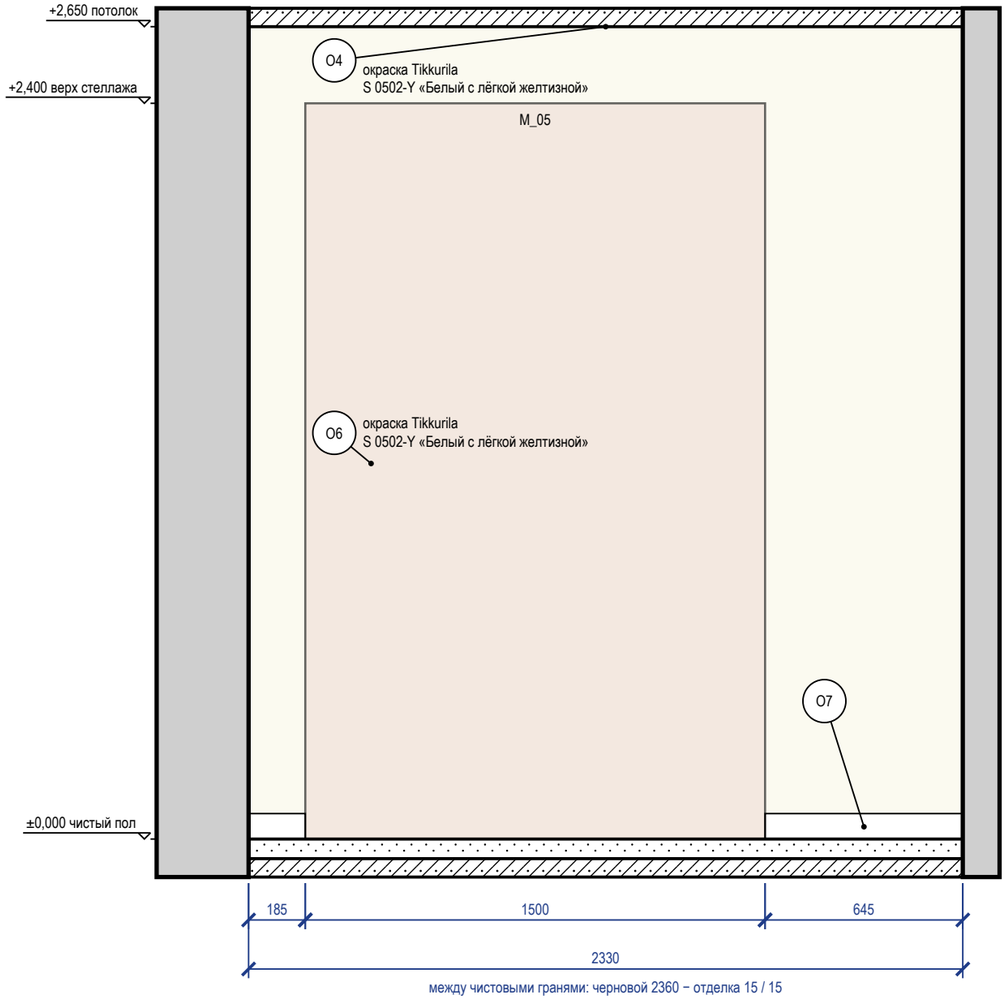

Развёртка стены В


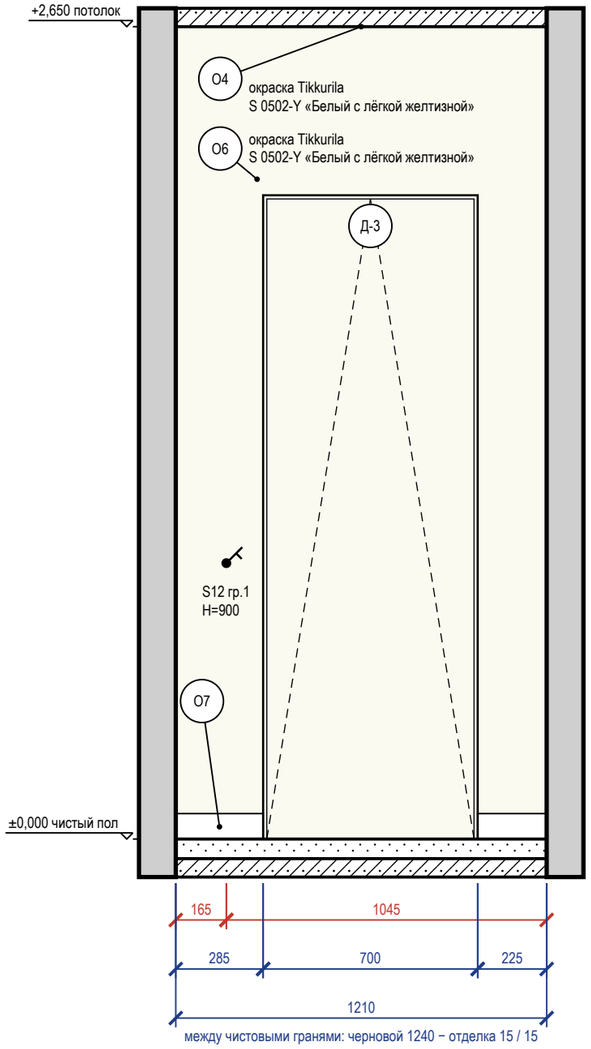


Схема разверток (М 1:100)

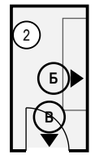

Ведомость отделки (на листе)

Марка	Поверхность	Материал, изделие	Цвет, код	Кол.
О4	потолок	окраска, Tikkurila Anti-Reflex 2, глубокоматовая, подготовка Q3	NCS S 0502-Y «Белый с лёгкой желтизной»	2,9 м²
О6	стены	окраска, Tikkurila Harmony, матовая, подготовка Q3	NCS S 0502-Y «Белый с лёгкой желтизной»	7,9 м²
О7	плинтус	плинтус МДФ, h 83 мм, Ultrawood Base 5340, ЛДФ под окраску, 83×15 мм, 2440 мм (арт. LDF-BASE-5340)	NCS S 0502-Y «Белый с лёгкой желтизной»	1,3 м

Примечания

1. Размеры — в мм от чистовых поверхностей стен; условные обозначения и общие указания — лист 3.
2. Двери скрытого монтажа — полотно в плоскости стены, отделка стены по полотну, плинтус прерывается у короба (узел — на листе узлов).

					Проект: Квартира 103 м²	М 1:20
	Лист	№ док.	Подпись	Дата	Развёртки стен. Кладовая (пом. 2)	Стадия / Лист / Листов
Дизайнер	Кырлан А.С.			04.11.26		П / 50 / 96

Развёртка стены А


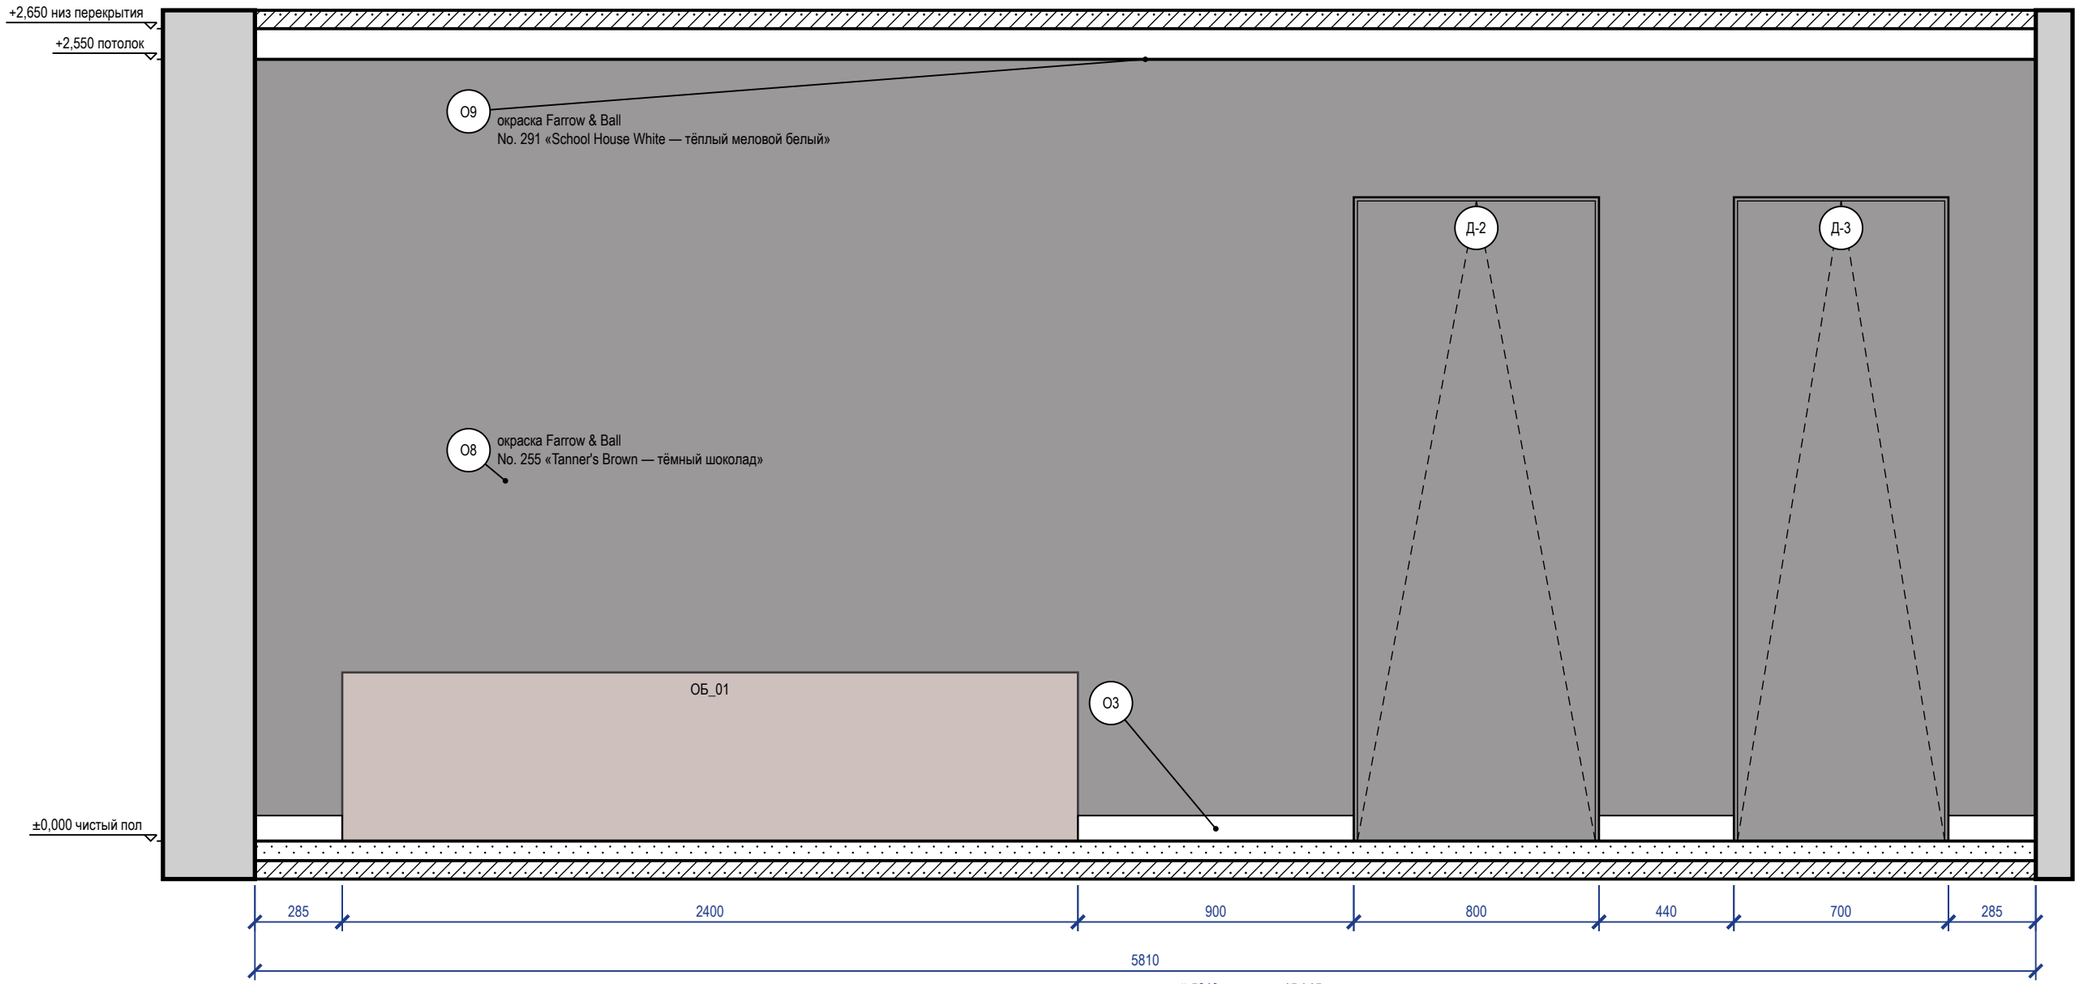


Схема развёрток (М 1:100)

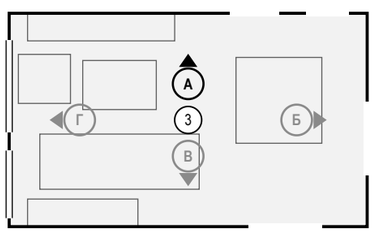

Ведомость отделки (на листе)

Марка	Поверхность	Материал, изделие	Цвет, код	Кол.
О3	плинтус	плинтус МДФ, h 83 мм, Ultrawood Base 5340, ЛДФ под окраску, 83×15 мм, 2440 мм (арт. LDF-BASE-5340), полуглянцевая	Farrow & Ball No. 291 «School House White тёплый меловой белый»	1,9 м
О8	акцентная стена	окраска, Farrow & Ball Modern Emulsion, аналог: интерьерная краска Farrow & Ball Modern Emulsion в цвете веера No. 255, матовая, матовая, подготовка К3	Farrow & Ball No. 255 «Tanner's Brown — тёмный шоколад»	11,7 м²
О9	потолок	окраска, Farrow & Ball Modern Emulsion, матовая, подготовка Q3	Farrow & Ball No. 291 «School House White тёплый меловой белый»	20,3 м²

Примечания

1. Размеры — в мм от чистовых поверхностей стен; условные обозначения и общие указания — лист 3.
2. Стена А показана двумя видами: здесь — архитектурная развёртка (мебель, отделка, проёмы, высоты), электроточки и выводы ВК с привязками и таблицей — на листе 52 («Привязки»).
3. Двери скрытого монтажа — полотно в плоскости стены, отделка стены по полотну, плинтус прерывается у короба (узел — на листе узлов).

					Проект: Квартира 103 м²	М 1:20
	Лист	№ док.	Подпись	Дата		
Дизайнер	Кырлан А.С.			04.11.26	Развёртка стены А. Гостиная-столовая (пом. 3)	Стадия: П; Лист: 51; Листов: 96

Развёртка стены А: электроточки и выводы

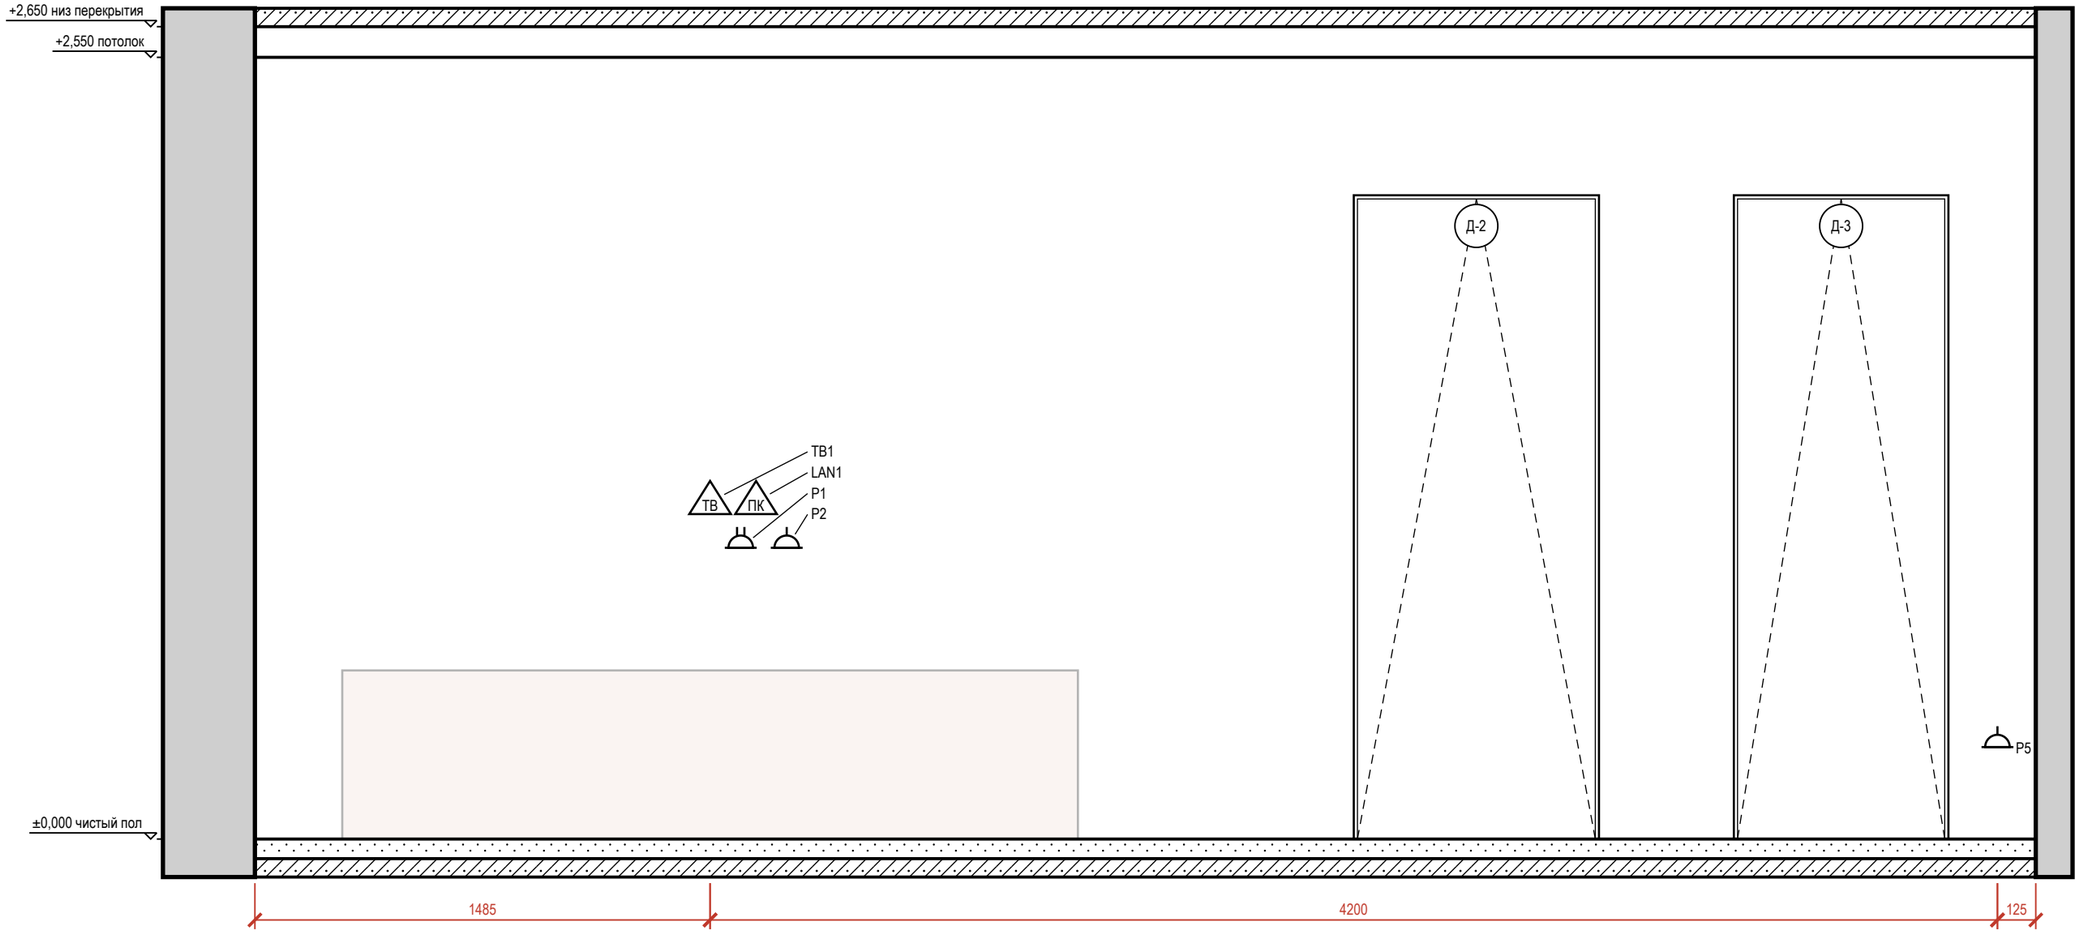



Таблица привязок электроточек и выводов

Марка	Назначение	От угла, мм	H от пола, мм	Примечание
TB1	розетка ТВ: ТВ-зона	1485	1100	
P1	розетка: ТВ-зона: телевизор, медиаплеер	1585	950	рамка 2 поста, гр. 5
LAN1	розетка RJ45: ТВ-зона: Smart TV	1635	1100	
P2	розетка: ТВ-зона: саундбар	1735	950	гр. 5
P5	розетка: обеденная зона, буфет M_10	5685	300	гр. 5

Условные обозначения

- розетка с заземляющим контактом; у знака — марка, ×N постов в рамке, гр. — группа щита, H — высота оси, мм
- ПК — розетка компьютерная RJ45
- ТВ — розетка телевизионная
- привязки точек и выводов от угла и от пола, мм
- A — марка развёртки: буква стены, стрелка — взгляд

Схема развёрток (М 1:100)

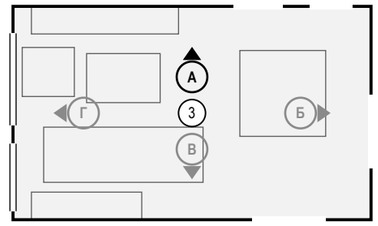

Примечания

1. Вид «Привязки» стены А — электроточки и выводы ВК; архитектурная развёртка (мебель, отделка, проёмы, высоты) — на листе 51. Мебель и приборы — подложкой для ориентира; их марки и обозначения мебели, проёмов и стен — там же.
2. Привязки — в мм: по горизонтали от левого чистового угла стены до оси изделия, H — от чистого пола до оси; все точки — в таблице привязок. Красная цепочка — привязки по осям; точки ближе 120 мм одна к другой в цепочку не дробятся — их привязки только в таблице.
3. У знака — марка электроточки (Р — розетка, S — выключатель, Св — светильник, ЭВ — вывод кабеля); условные обозначения и общие указания — лист 3.

					Проект: Квартира 103 м² — М 1:20
	Лист	№ док.	Подпись	Дата	
Дизайнер	Кырлан А.С.			04.11.26	Привязки электроточек, стена А. Гостиная-столовая (пом. 3)

Стадия	Лист	Листов
П	52	96

Развёртка стены Б


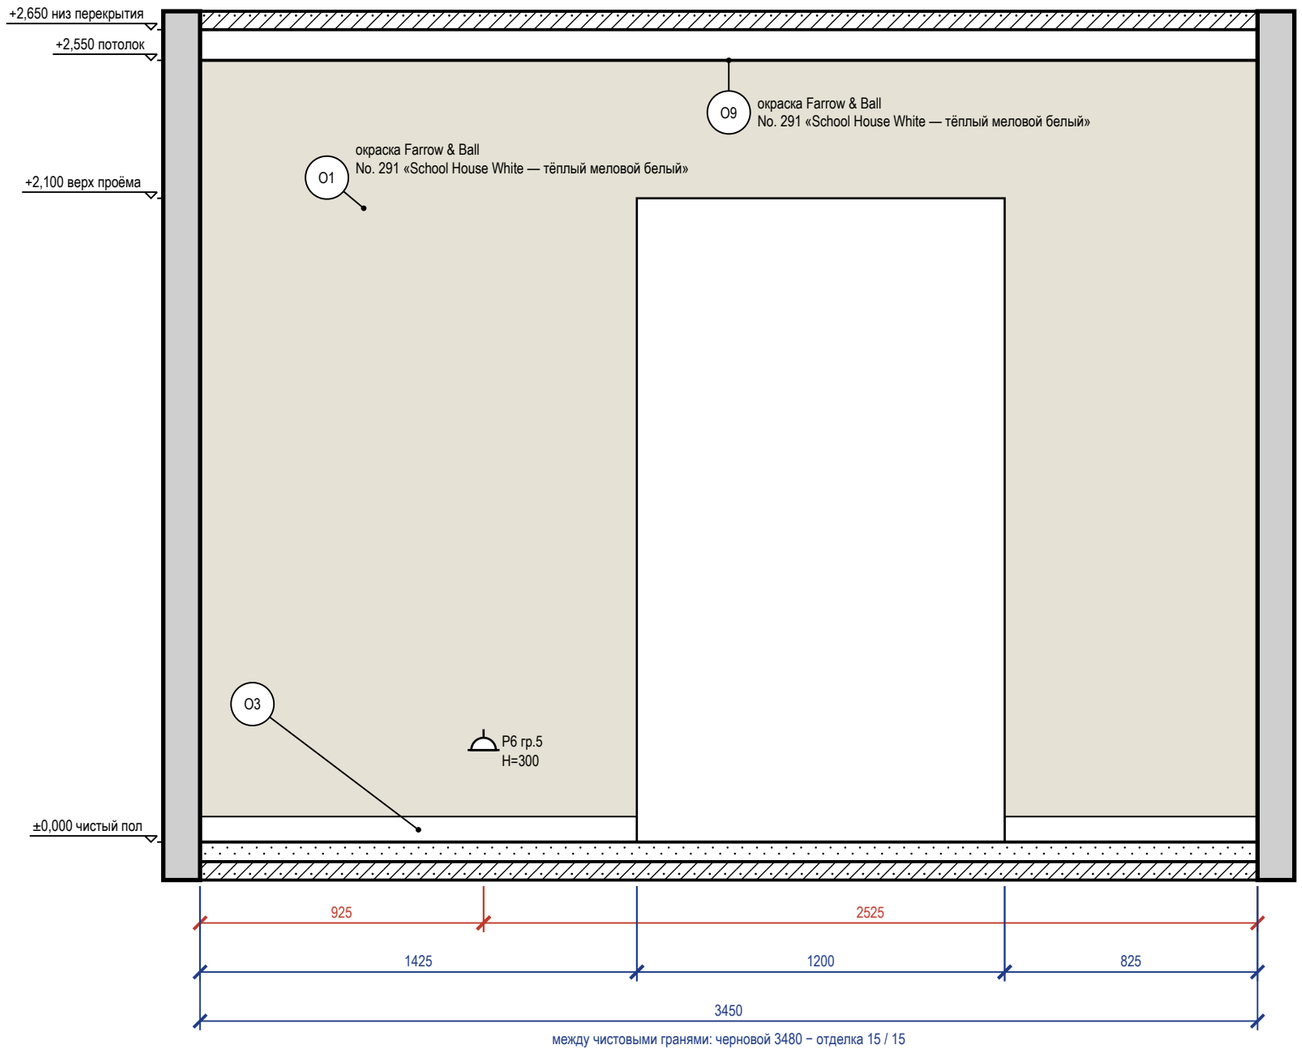


Схема развёрток (М 1:100)

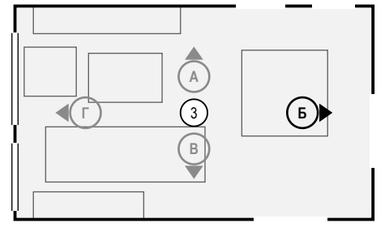

Ведомость отделки (на листе)


Марка	Поверхность	Материал, изделие	Цвет, код	Кол.
O1	стены	окраска, Farrow & Ball Modern Emulsion, матовая, подготовка K3	Farrow & Ball No. 291 «School House White — тёплый меловой белый»	6,3 м²
O3	плинтус	плинтус МДФ, h 83 мм, Ultrawood Base 5340, ЛДФ под окраску, 83×15 мм, 2440 мм (арт. LDF-BASE-5340), полуглянцевая	Farrow & Ball No. 291 «School House White — тёплый меловой белый»	2,3 м
O9	потолок	окраска, Farrow & Ball Modern Emulsion, матовая, подготовка Q3	Farrow & Ball No. 291 «School House White — тёплый меловой белый»	20,3 м²

Примечания

1. Размеры — в мм от чистовых поверхностей стен; условные обозначения и общие указания — лист 3.


					Проект: Квартира 103 м²		М 1:20
	Лист	№ док.	Подпись	Дата	Развёртка стены Б. Гостиная-столовая (пом. 3)	Стадия	Лист	Листов
Дизайнер	Кырлан А.С.			04.11.26		П	53	96

Развёртка стены В

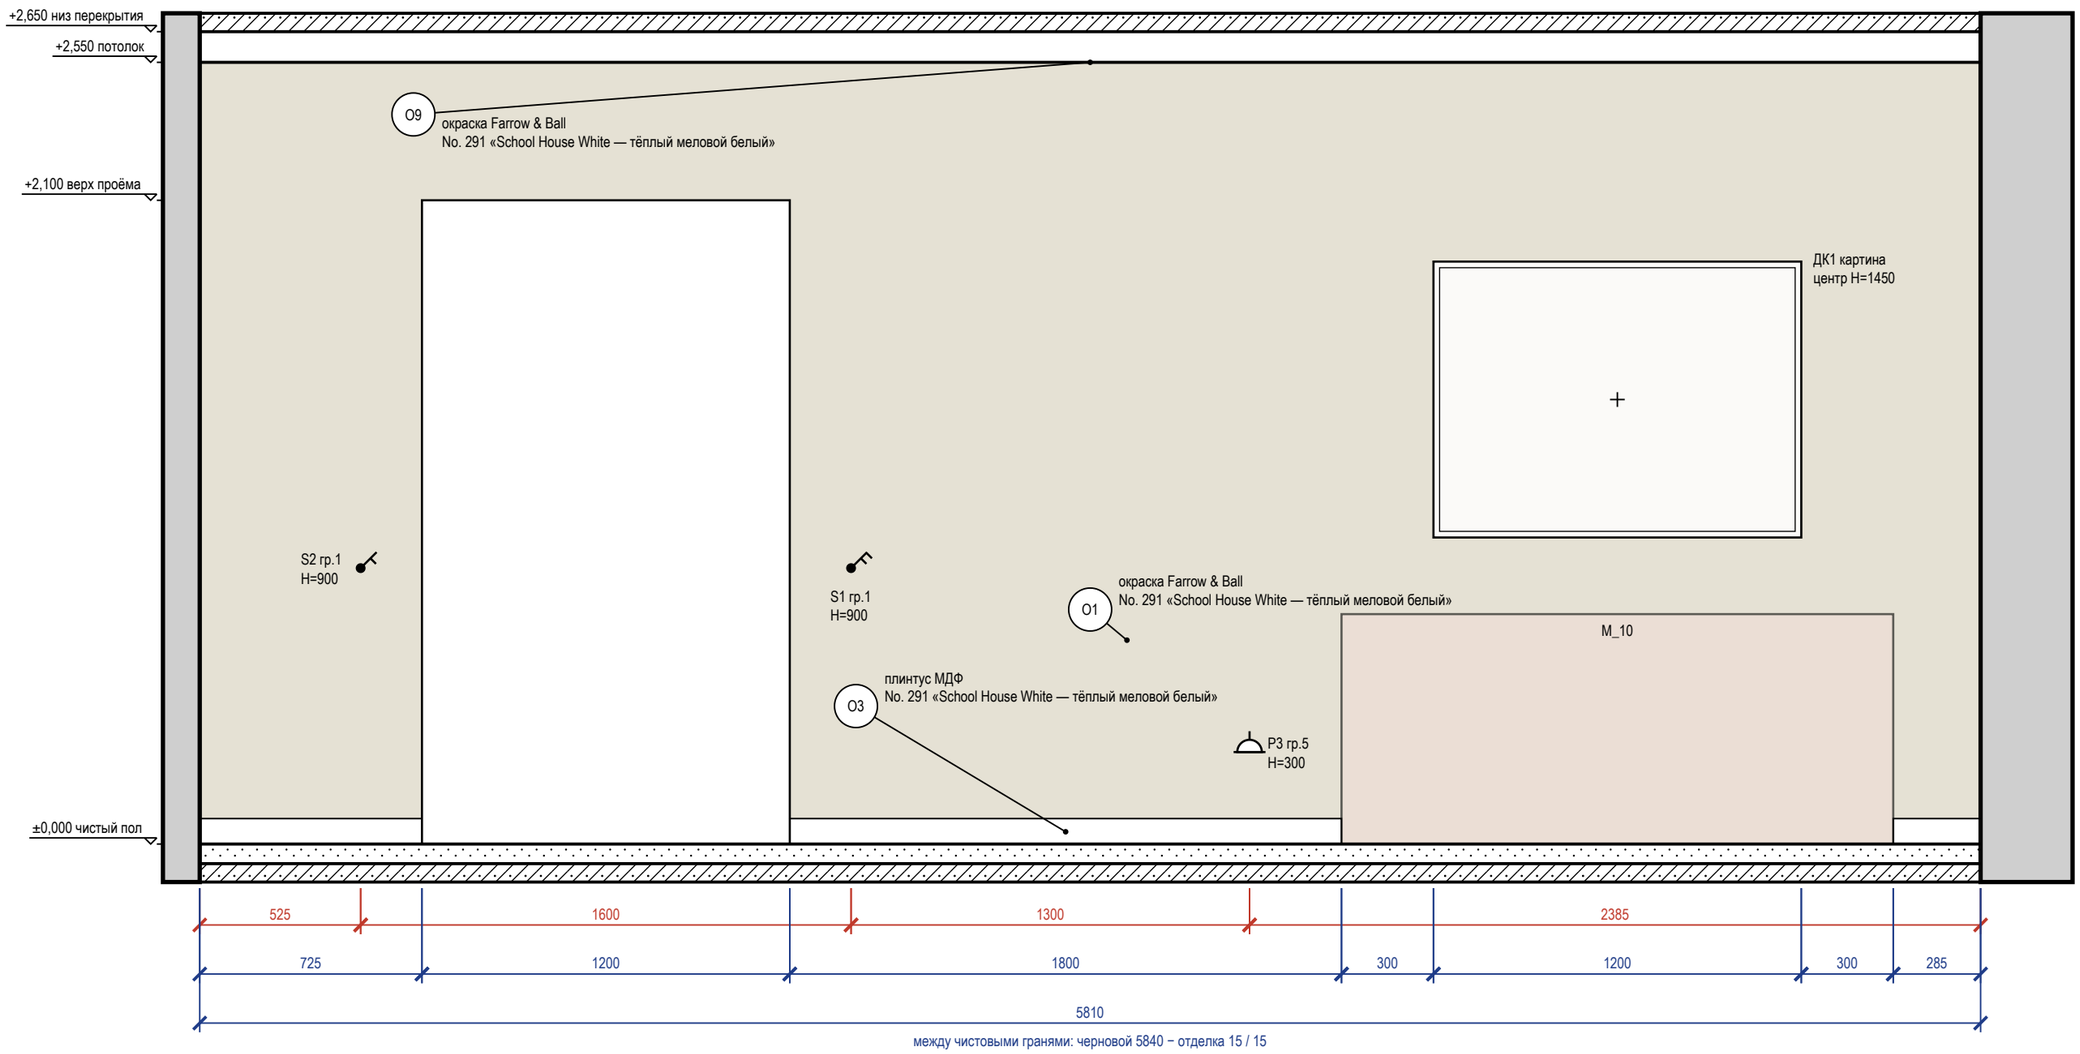

между чистовыми гранями: черновой 5840 − отделка 15 / 15

Схема развёрток (М 1:100)

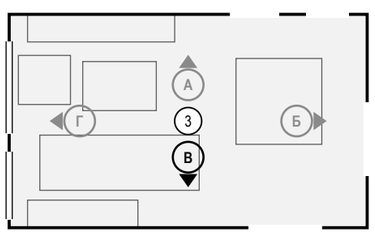

Ведомость отделки (на листе)

Марка	Поверхность	Материал, изделие	Цвет, код	Кол.
О1	стены	окраска, Farrow & Ball Modern Emulsion, матовая, подготовка К3	Farrow & Ball No. 291 «School House White тёплый меловой белый»	12,3 м²
О3	плинтус	плинтус МДФ, h 83 мм, Ultrawood Base 5340, ЛДФ под окраску, 83×15 мм, 2440 мм (арт. LDF-BASE-5340), полуглянцевая	Farrow & Ball No. 291 «School House White тёплый меловой белый»	2,8 м
О9	потолок	окраска, Farrow & Ball Modern Emulsion, матовая, подготовка Q3	Farrow & Ball No. 291 «School House White тёплый меловой белый»	20,3 м²

Примечания

1. Размеры — в мм от чистовых поверхностей стен; условные обозначения и общие указания — лист 3.
2. Картины и зеркала крепить к основанию по паспорту изделия (закладные и анкеры — в перечне скрытых работ); крест — ось центра предмета.

					Проект: Квартира 103 м² — М 1:20
	Лист	№ док.	Подпись	Дата	Развёртка стены В. Гостиная-столовая (пом. 3)
Дизайнер	Кырлан А.С.			04.11.26	Стадия: П; Лист: 54; Листов: 96

выпуск 04.11.2026 № d6a6e88d · стр. 54 из 96

Развёртка стены Г


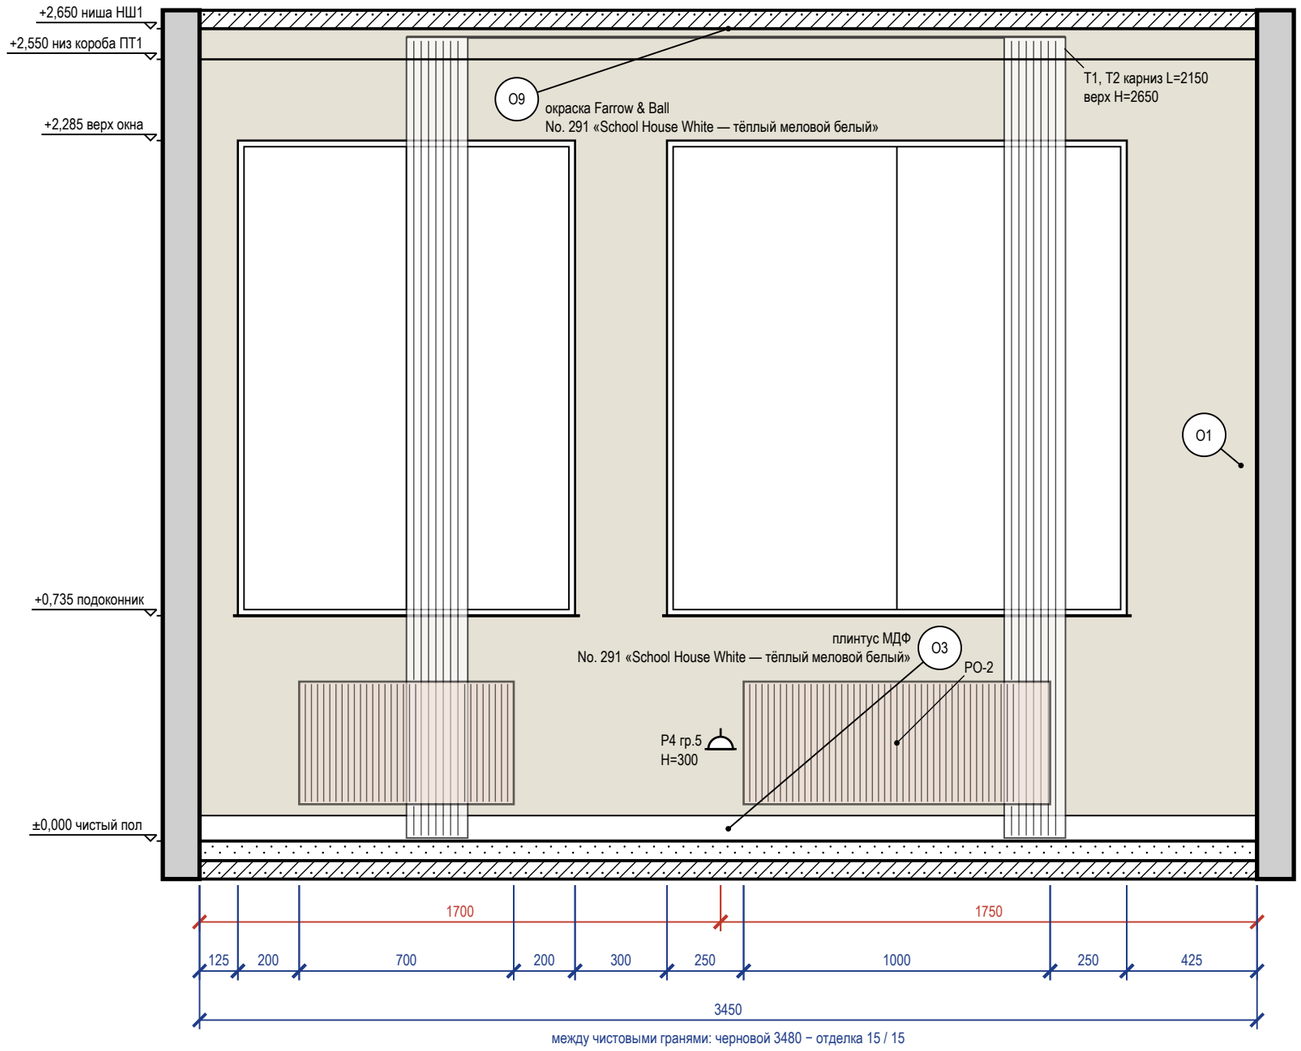


Схема развёрток (М 1:100)

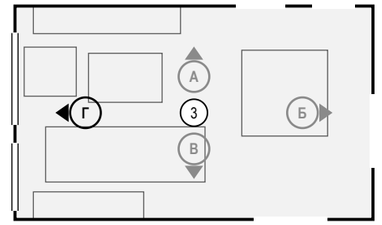

Ведомость отделки (на листе)

Марка	Поверхность	Материал, изделие	Цвет, код	Кол.
О1	стены	окраска, Farrow & Ball Modern Emulsion, матовая, подготовка К3	Farrow & Ball No. 291 «School House White — тёплый меловой белый»	5,1 м²
О3	плинтус	плинтус МДФ, h 83 мм, Ultrawood Base 5340, ЛДФ под окраску, 83×15 мм, 2440 мм (арт. LDF-BASE-5340), полуглянцевая	Farrow & Ball No. 291 «School House White — тёплый меловой белый»	3,5 м
О9	потолок	окраска, Farrow & Ball Modern Emulsion, матовая, подготовка Q3	Farrow & Ball No. 291 «School House White — тёплый меловой белый»	20,3 м²

Примечания

1. Размеры — в мм от чистовых поверхностей стен; условные обозначения и общие указания — лист 3.
2. Карнизы (шины) — по ведомости текстиля декоратора: длина L и верх H на развёртке — те же числа, что в ведомости; крепление — до окраски потолка.
3. Линии узора (швы плитки, складки штор, рёбра радиаторов) прерываются у знаков и выносок — просвет между линиями не менее 0,7 мм.

	Лист	№ док.	Подпись	Дата
Дизайнер	Кырлан А.С.			04.11.26

Проект: Квартира 103 м² — **М 1:20**

Развёртка стены Г.
Гостиная-столовая (пом. 3)

Стадия	Лист	Листов
П	55	96

Развёртка стены А


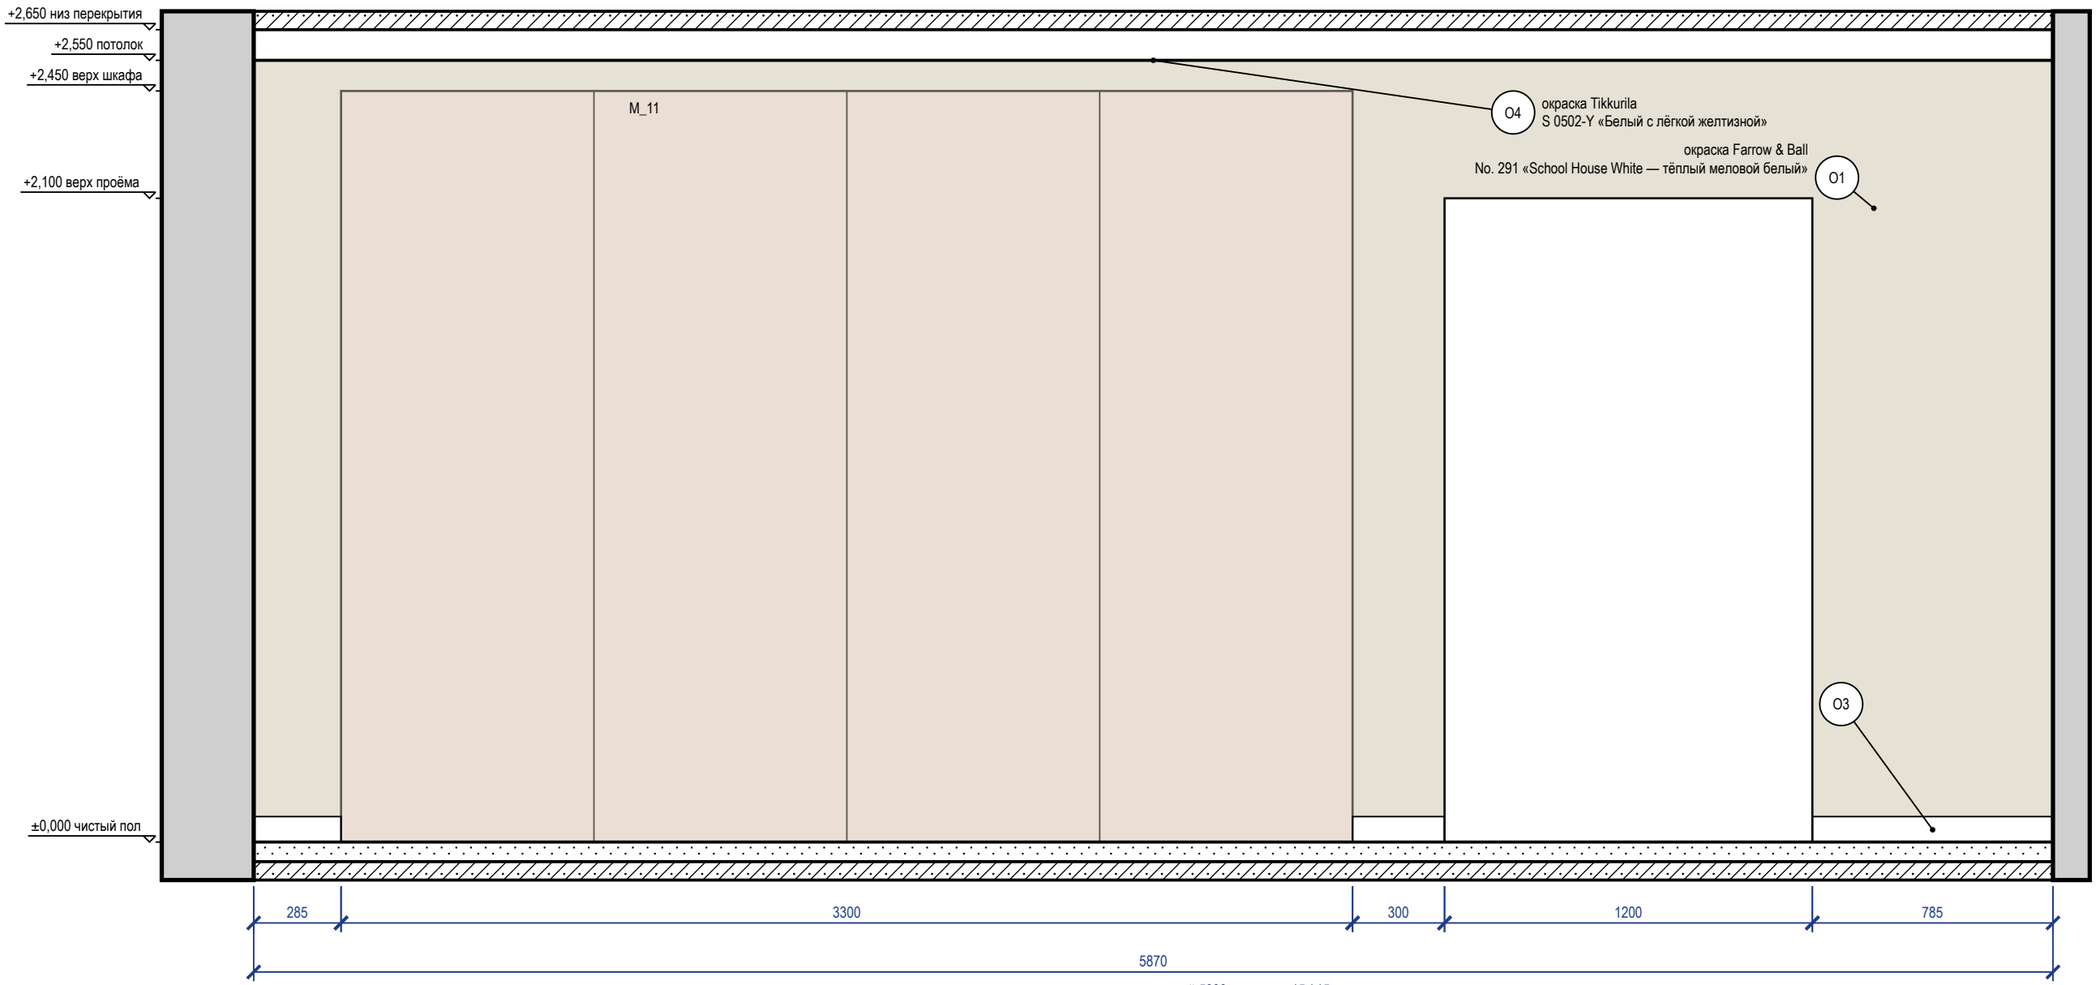


Схема развёрток (М 1:100)

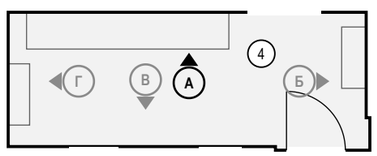

Ведомость отделки (на листе)

Марка	Поверхность	Материал, изделие	Цвет, код	Кол.
O1	стены	окраска, Farrow & Ball Modern Emulsion, матовая, подготовка Q3	Farrow & Ball No. 291 «School House White тёплый меловой белый»	12,4 м²
O3	плинтус	плинтус МДФ, h 83 мм, Ultrawood Base 5340, ЛДФ под окраску, 83×15 мм, 2440 мм (арт. LDF-BASE-5340)	Farrow & Ball No. 291 «School House White тёплый меловой белый»	1,4 м
O4	потолок	окраска, Tikkurila Anti-Reflex 2, глубокоматовая, подготовка Q3	NCS S 0502-Y «Белый с лёгкой желтизной»	12,9 м²


Примечания

1. Размеры — в мм от чистовых поверхностей стен; условные обозначения и общие указания — лист 3.

					Проект: Квартира 103 м²	М 1:20
	Лист	№ док.	Подпись	Дата		
Дизайнер	Кырлан А.С.			04.11.26	Развёртка стены А. Прихожая-холл (пом. 4)	Стадия: П; Лист: 56; Листов: 96


выпуск 04.11.2026 № d6a6e5e88d · стр. 56 из 96

Развёртка стены Б

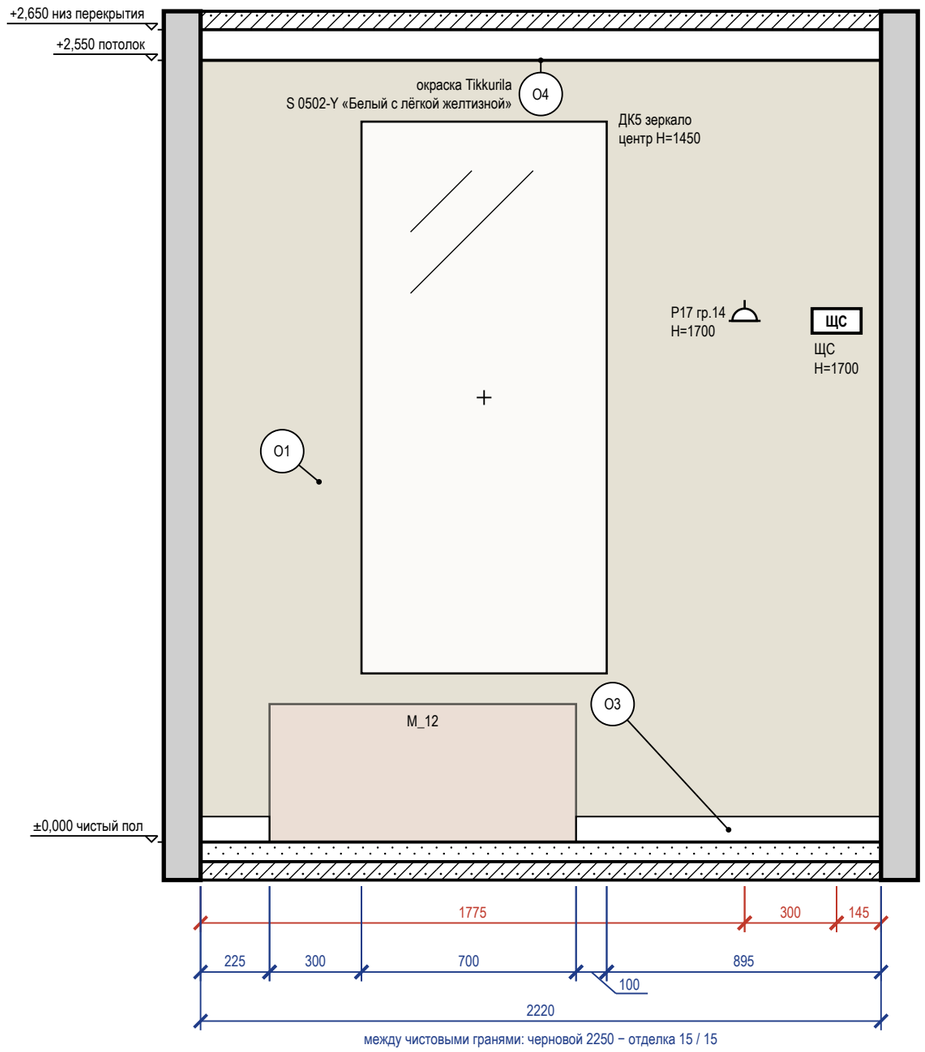


между чистовыми гранями: черновой 2250 − отделка 15 / 15

Развёртка стены Г

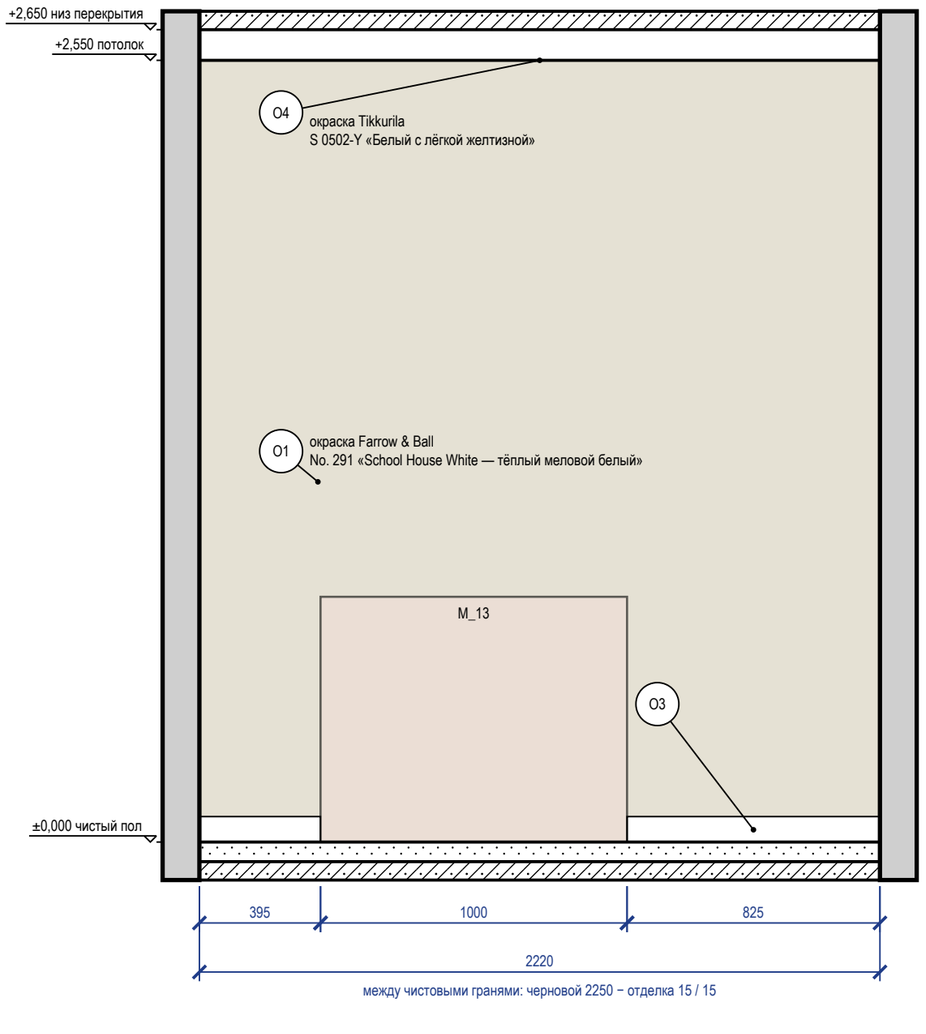

между чистовыми гранями: черновой 2250 − отделка 15 / 15

Схема развёрток (М 1:100)

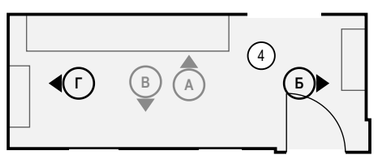

Ведомость отделки (на листе)

Марка	Поверхность	Материал, изделие	Цвет, код	Кол.
О1	стены	окраска, Farrow & Ball Modern Emulsion, матовая, подготовка Q3	Farrow & Ball No. 291 «School House White тёплый меловой белый»	11,3 м²
О3	плинтус	плинтус МДФ, h 83 мм, Ultrawood Base 5340, ЛДФ под окраску, 83×15 мм, 2440 мм (арт. LDF-BASE-5340)	Farrow & Ball No. 291 «School House White тёплый меловой белый»	2,4 м
О4	потолок	окраска, Tikkurila Anti-Reflex 2, глубокоматовая, подготовка Q3	NCS S 0502-Y «Белый с лёгкой желтизной»	12,9 м²

Примечания

1. Размеры — в мм от чистовых поверхностей стен; условные обозначения и общие указания — лист 3.
2. Картины и зеркала крепить к основанию по паспорту изделия (закладные и анкеры — в перечне скрытых работ); крест — ось центра предмета.

	Лист	№ док.	Подпись	Дата
Дизайнер	Кырлан А.С.			04.11.26

Проект: Квартира 103 м² — **М 1:20**

Развёртки стен Б, Г.
Прихожая-холл (пом. 4)

Стадия	Лист	Листов
П	57	96

Развёртка стены В


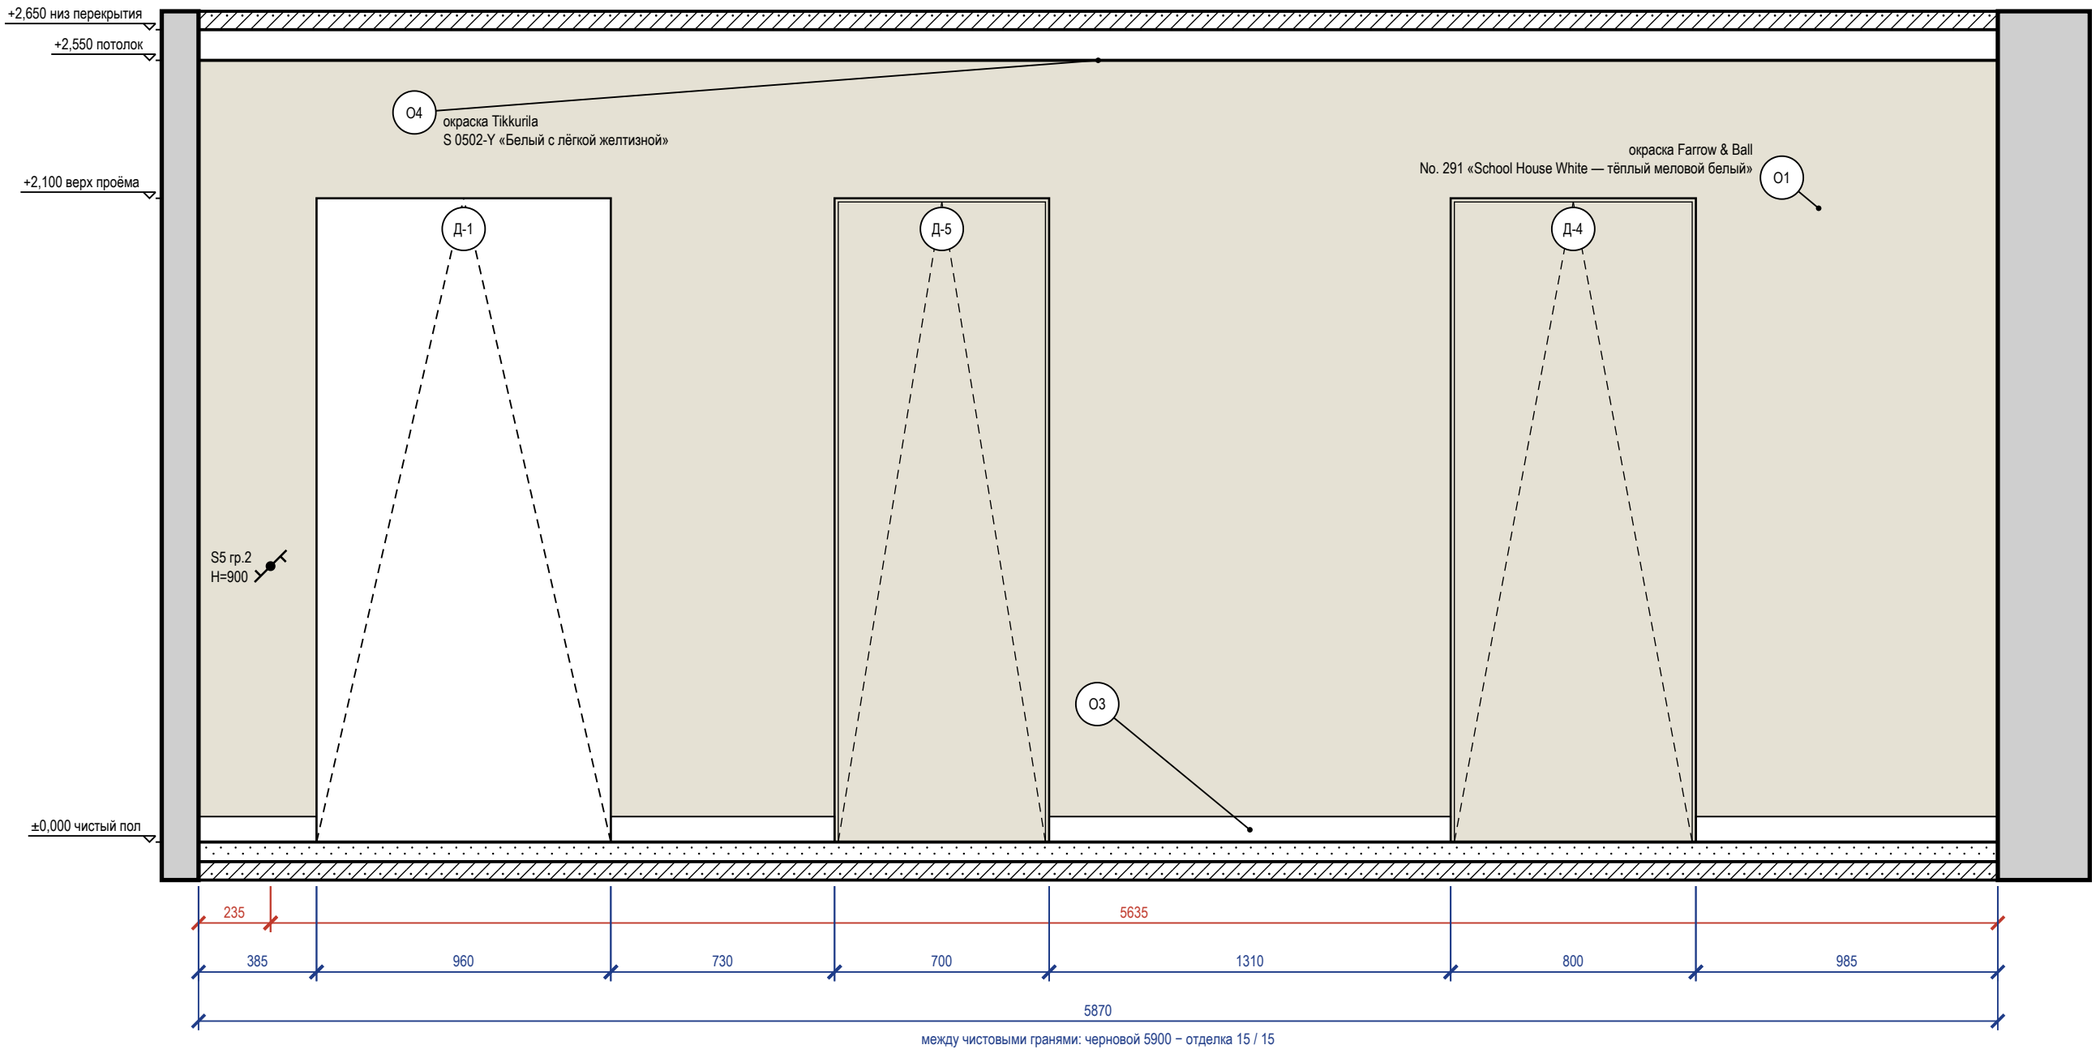


Схема развёрток (М 1:100)

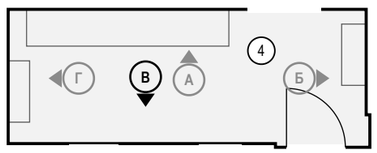

Ведомость отделки (на листе)

Марка	Поверхность	Материал, изделие	Цвет, код	Кол.
О1	стены	окраска, Farrow & Ball Modern Emulsion, матовая, подготовка Q3	Farrow & Ball No. 291 «School House White тёплый меловой белый»	9,8 м²
О3	плинтус	плинтус МДФ, h 83 мм, Ultrawood Base 5340, ЛДФ под окраску, 83×15 мм, 2440 мм (арт. LDF-BASE-5340)	Farrow & Ball No. 291 «School House White тёплый меловой белый»	3,4 м
О4	потолок	окраска, Tikkurila Anti-Reflex 2, глубокоматовая, подготовка Q3	NCS S 0502-Y «Белый с лёгкой желтизной»	12,9 м²

Примечания

1. Размеры — в мм от чистовых поверхностей стен; условные обозначения и общие указания — лист 3.
2. Двери скрытого монтажа — полотно в плоскости стены, отделка стены по полотну, плинтус прерывается у короба (узел — на листе узлов).

					Проект: Квартира 103 м²	М 1:20
	Лист	№ док.	Подпись	Дата		
Дизайнер	Кырлан А.С.			04.11.26	Развёртка стены В. Прихожая-холл (пом. 4)	Стадия: П; Лист: 58; Листов: 96

Развёртка стены Б


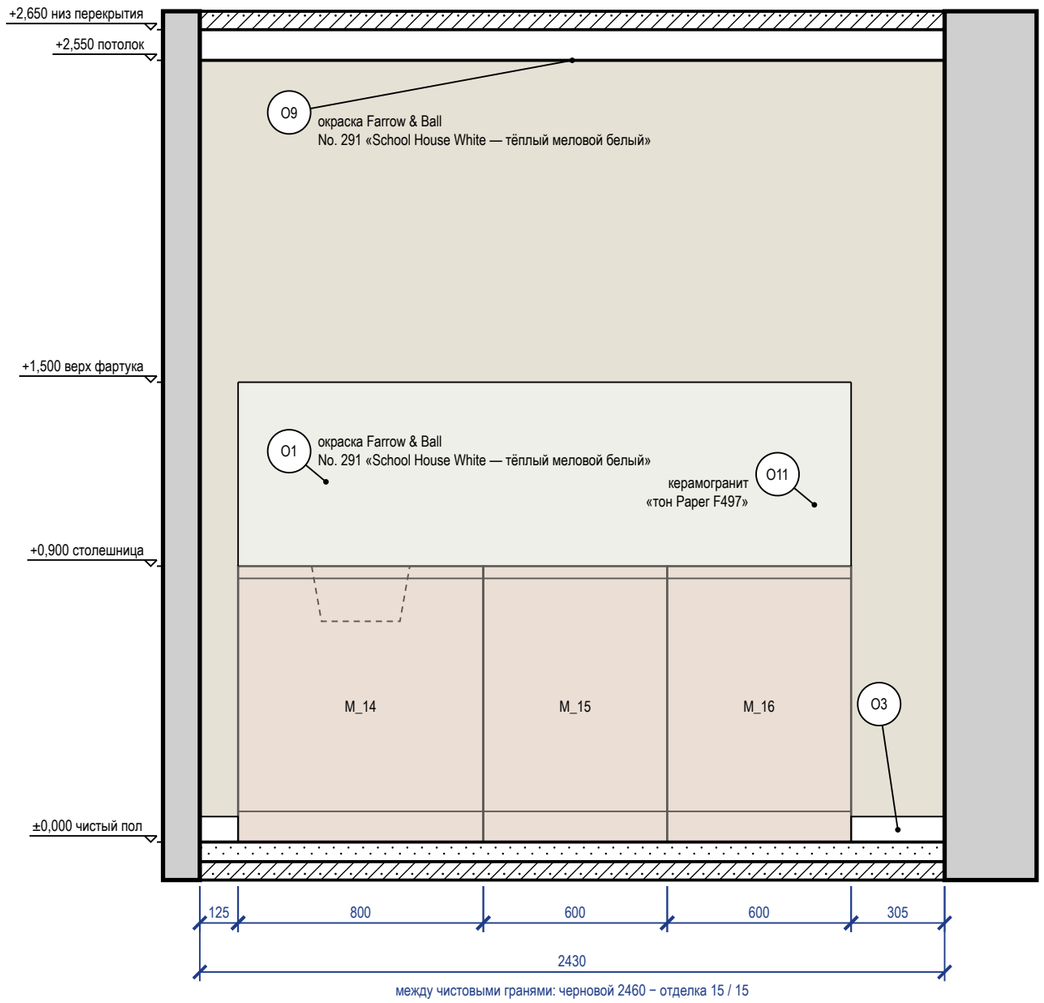


Схема развёрток (М 1:100)

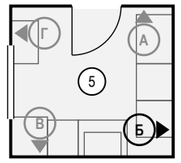

Ведомость отделки (на листе)

Марка	Поверхность	Материал, изделие	Цвет, код	Кол.
О1	стены	окраска, Farrow & Ball Modern Emulsion, матовая, подготовка К3	Farrow & Ball No. 291 «School House White — тёплый меловой белый»	5 м²
О3	плинтус	плинтус МДФ, h 83 мм, Ultrawood Base 5340, ЛДФ под окраску, 83×15 мм, 2440 мм (арт. LDF-BASE-5340), полуглянцевая	Farrow & Ball No. 291 «School House White — тёплый меловой белый»	0,4 м
О9	потолок	окраска, Farrow & Ball Modern Emulsion, матовая, подготовка Q3	Farrow & Ball No. 291 «School House White — тёплый меловой белый»	6,5 м²
О11	фартук	керамогранит, аналог: керамогранит матовый, тон F497, затирка CG2WA	#F1F1EC «тон Paper F497»	1,2 м²

Примечания

1. Размеры — в мм от чистовых поверхностей стен; условные обозначения и общие указания — лист 3.
2. Стена Б показана двумя видами: здесь — архитектурная развёртка (мебель, отделка, проёмы, высоты), электроточки и выводы ВК с привязками и таблицей — на листе 60 («Привязки»).

					Проект: Квартира 103 м²	М 1:20
	Лист	№ док.	Подпись	Дата	Развёртка стены Б. Кухня (пом. 5), кухонный фронт	Стадия / Лист / Листов
Дизайнер	Кырлан А.С.			04.11.26		П / 59 / 96

Развёртка стены Б: электроточки и выводы

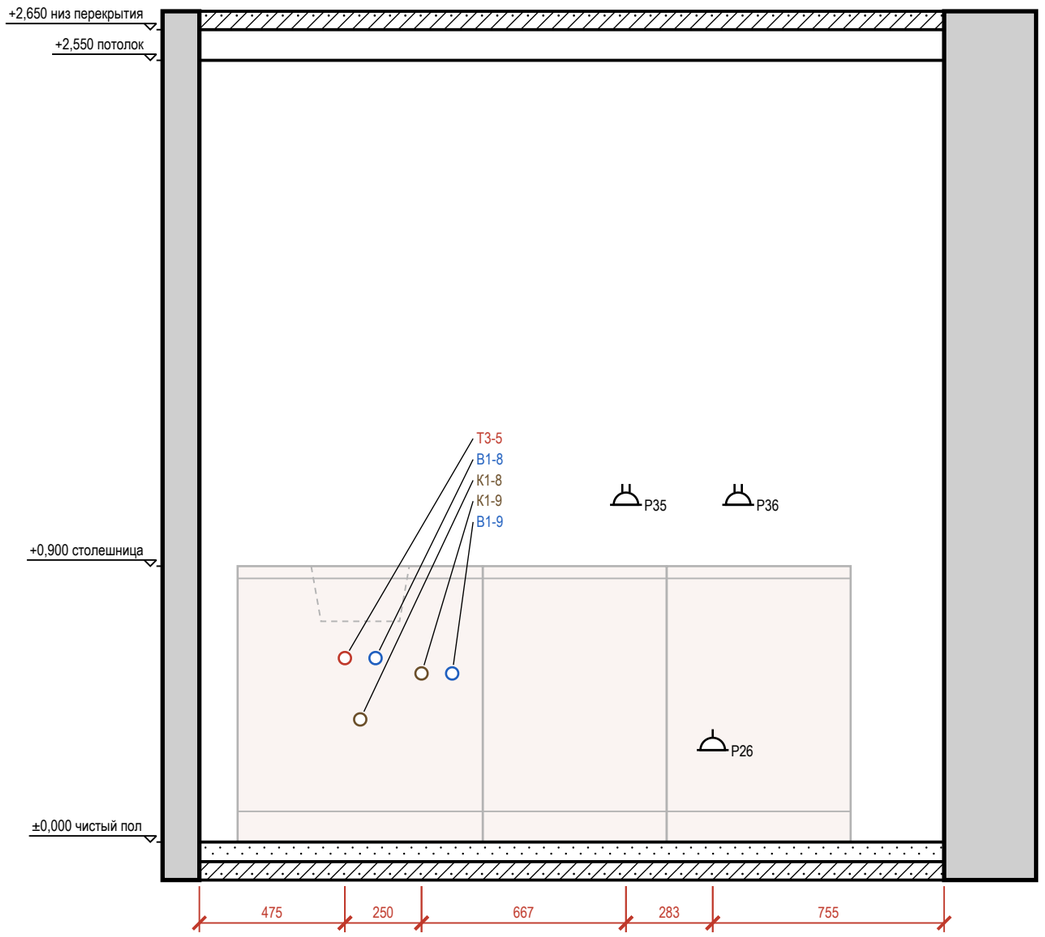



Таблица привязок электроточек и выводов

Марка	Назначение	От угла, мм	H от пола, мм	Примечание
T3-5	горячая вода — мойка кухонная	475	600	межос. 100
K1-8	канализация — мойка кухонная	525	400	Ø50
B1-8	холодная вода — мойка кухонная	575	600	межос. 100
K1-9	канализация — посудомоечная машина	725	550	Ø40; слив ПММ в шкафу мойки
B1-9	холодная вода — посудомоечная машина	825	550	кран ПММ в шкафу мойки
P35	розетка: фартук	1392	1100	рамка 2 поста, гр. 9
P26	розетка: посудомоечная машина — в соседнем модуле, за ящиком	1675	300	гр. 13
P36	розетка: фартук	1758	1100	рамка 2 поста, гр. 9

Условные обозначения

- розетка с заземляющим контактом; у знака — марка, ×N постов в рамке, гр. — группа щита, H — высота оси, мм
- вывод B1 (код — в ведомости привязок)
- вывод T3 (код — в ведомости привязок)
- вывод K1 (код — в ведомости привязок)
- привязки точек и выводов от угла и от пола, мм
- марка развёртки: буква стены, стрелка — взгляд

Схема развёрток (M 1:50)

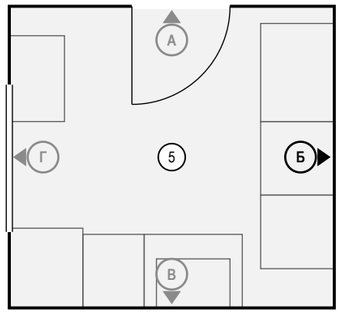

Примечания

1. Вид «Привязки» стены Б — электроточки и выводы ВК; архитектурная развёртка (мебель, отделка, проёмы, высоты) — на листе 59. Мебель и приборы — подложкой для ориентира; их марки и обозначения мебели, проёмов и стен — там же.
2. Привязки — в мм: по горизонтали от левого чистового угла стены до оси изделия, H — от чистого пола до оси; все точки — в таблице привязок. Красная цепочка — привязки по осям; точки ближе 120 мм одна к другой в цепочку не дробятся — их привязки только в таблице.
3. У знака — марка электроточки (P — розетка, S — выключатель, Св — светильник, ЭВ — вывод кабеля); условные обозначения и общие указания — лист 3.
4. Коды выводов ВК: B1 — холодная вода, T3 — горячая вода, K1 — канализация; номер после дефиса — номер вывода на листе выводов сантехники.
5. Выводы кухонной техники — по утверждённому проекту кухни: привязки выводов даются от осей модулей гарнитура.

					Проект: Квартира 103 м² — M 1:20
	Лист	№ док.	Подпись	Дата	Привязки электроточек и выводов ВК, стена Б. Кухня (пом. 5)
Дизайнер	Кырлан А.С.			04.11.26	

Стадия	Лист	Листов
П	60	96

Развёртка стены В


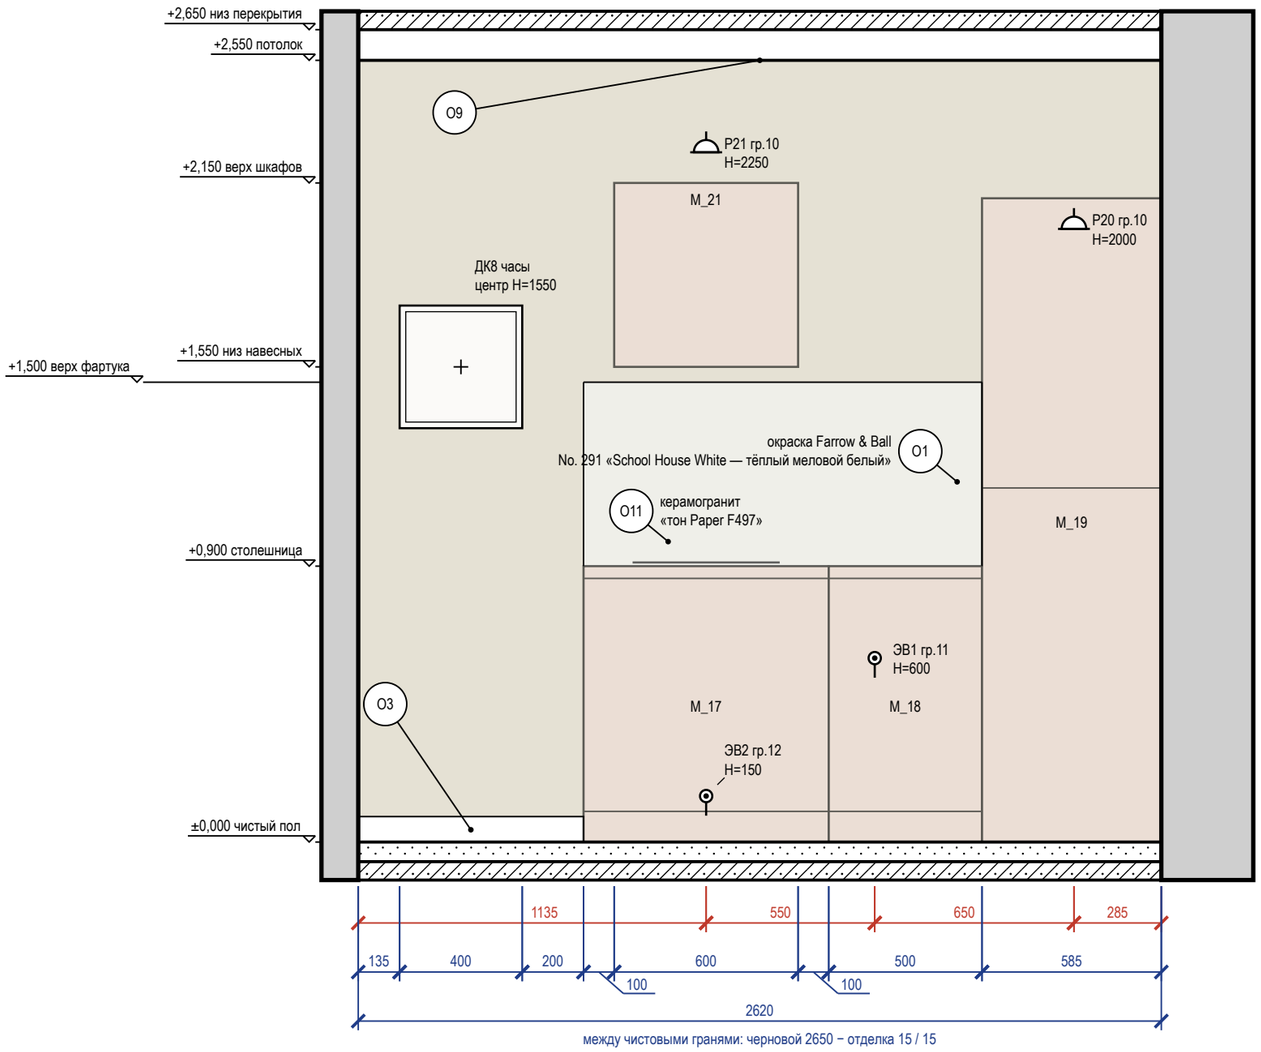


Схема развёрток (М 1:100)

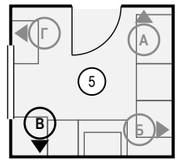

Ведомость отделки (на листе)


Марка	Поверхность	Материал, изделие	Цвет, код	Кол.
О1	стены	окраска, Farrow & Ball Modern Emulsion, матовая, подготовка К3	Farrow & Ball No. 291 «School House White — тёплый меловой белый»	5,9 м²
О3	плинтус	плинтус МДФ, h 83 мм, Ultrawood Base 5340, ЛДФ под окраску, 83×15 мм, 2440 мм (арт. LDF-BASE-5340), полуглянцевая	Farrow & Ball No. 291 «School House White — тёплый меловой белый»	0,7 м
О9	потолок	окраска, Farrow & Ball Modern Emulsion, матовая, подготовка Q3	Farrow & Ball No. 291 «School House White — тёплый меловой белый»	6,5 м²
О11	фартук	керамогранит, аналог: керамогранит матовый, тон F497, затирка CG2WA	#F1F1EC «тон Paper F497»	0,8 м²

Примечания

1. Размеры — в мм от чистовых поверхностей стен; условные обозначения и общие указания — лист 3.
2. Картины и зеркала крепить к основанию по паспорту изделия (закладные и анкеры — в перечне скрытых работ); крест — ось центра предмета.
3. Выводы кухонной техники — по утверждённому проекту кухни: привязки выводов даются от осей модулей гарнитура.


					Проект: Квартира 103 м²	М 1:20
	Лист	№ док.	Подпись	Дата	Развёртка стены В. Кухня (пом. 5), кухонный фронт	Стадия / Лист / Листов
Дизайнер	Кырлан А.С.			04.11.26		П / 61 / 96

Развёртка стены А

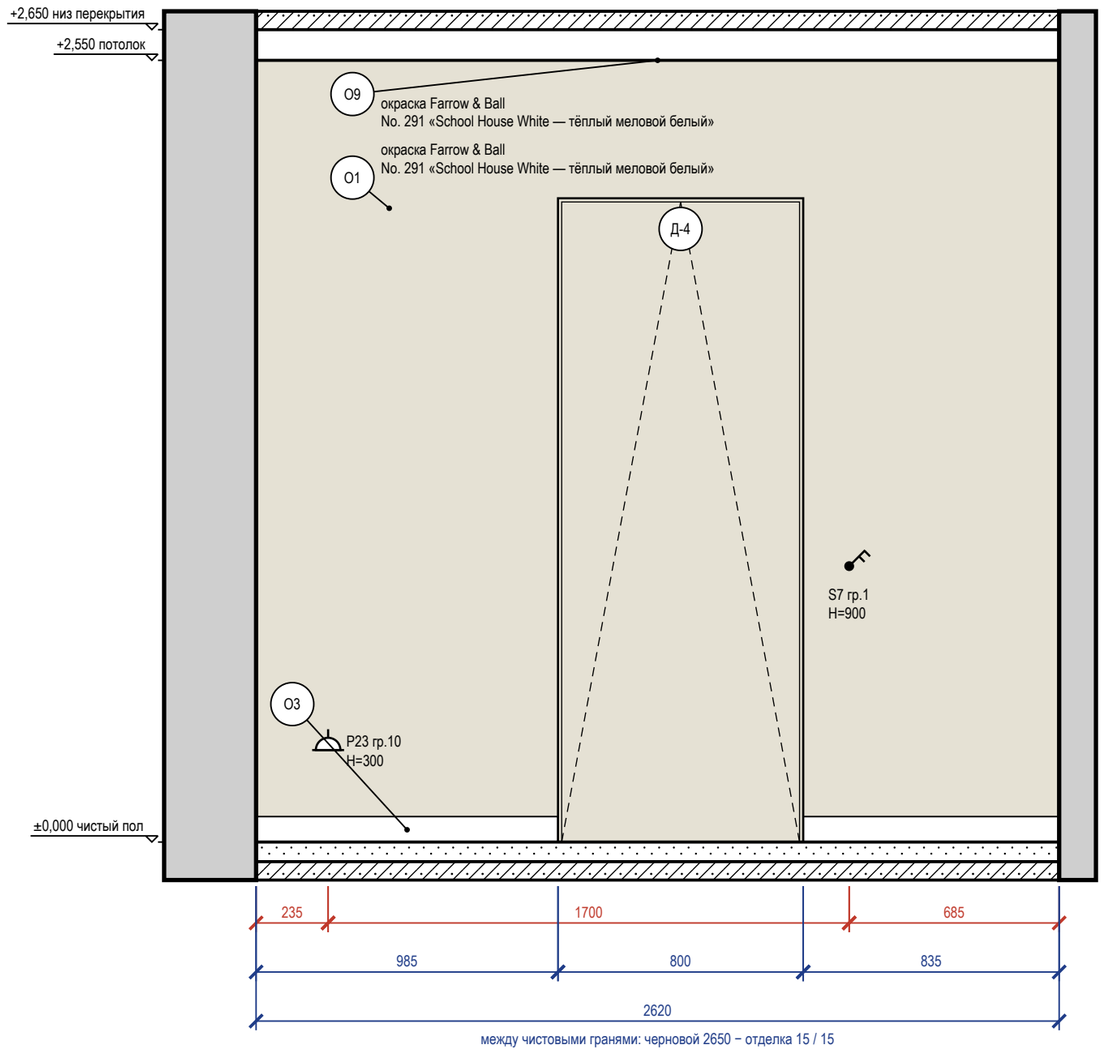


между чистовыми гранями: черновой 2650 − отделка 15 / 15

Развёртка стены Г

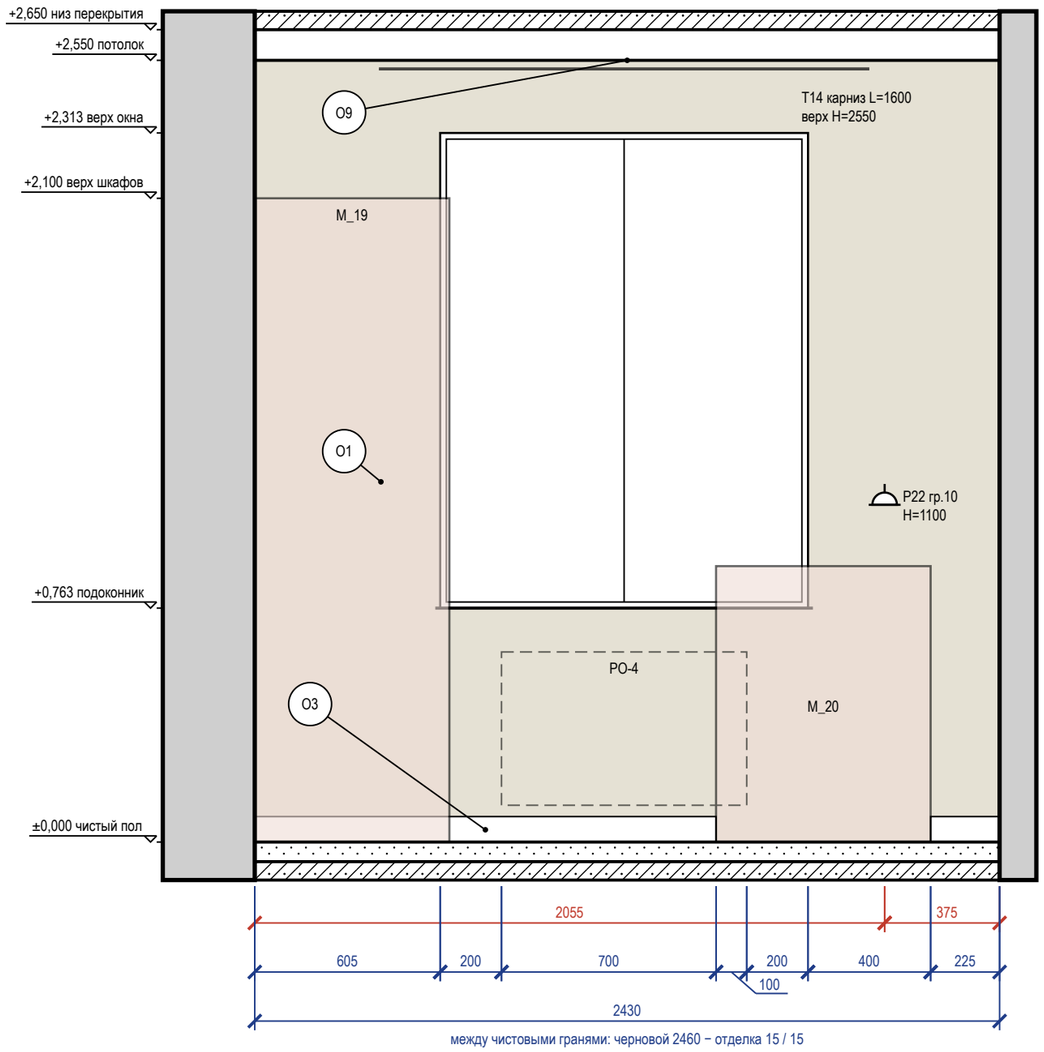

между чистовыми гранями: черновой 2460 − отделка 15 / 15

Схема развёрток (М 1:100)

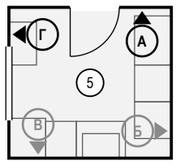

Ведомость отделки (на листе)

Марка	Поверхность	Материал, изделие	Цвет, код	Кол.
О1	стены	окраска, Farrow & Ball Modern Emulsion, матовая, подготовка К3	Farrow & Ball No. 291 «School House White тёплый меловой белый»	9,3 м²
О3	плинтус	плинтус МДФ, h 83 мм, Ultrawood Base 5340, ЛДФ под окраску, 83×15 мм, 2440 мм (арт. LDF-BASE-5340), полуглянцевая	Farrow & Ball No. 291 «School House White тёплый меловой белый»	3,5 м
О9	потолок	окраска, Farrow & Ball Modern Emulsion, матовая, подготовка Q3	Farrow & Ball No. 291 «School House White тёплый меловой белый»	6,5 м²

Примечания

1. Размеры — в мм от чистовых поверхностей стен; условные обозначения и общие указания — лист 3.
2. Карнизы (шины) — по ведомости текстиля декоратора: длина L и верх H на развёртке — те же числа, что в ведомости; крепление — до окраски потолка.
3. Двери скрытого монтажа — полотно в плоскости стены, отделка стены по полотну, плинтус прерывается у короба (узел — на листе узлов).

	Лист	№ док.	Подпись	Дата
Дизайнер	Кырлан А.С.			04.11.26


Проект: Квартира 103 м² — **М 1:20**

Развёртки стен А, Г. Кухня (пом. 5)

Стадия	Лист	Листов
П	62	96


выпуск 04.11.2026 № d6a6e5e88d · стр. 62 из 96

Развёртка стены А

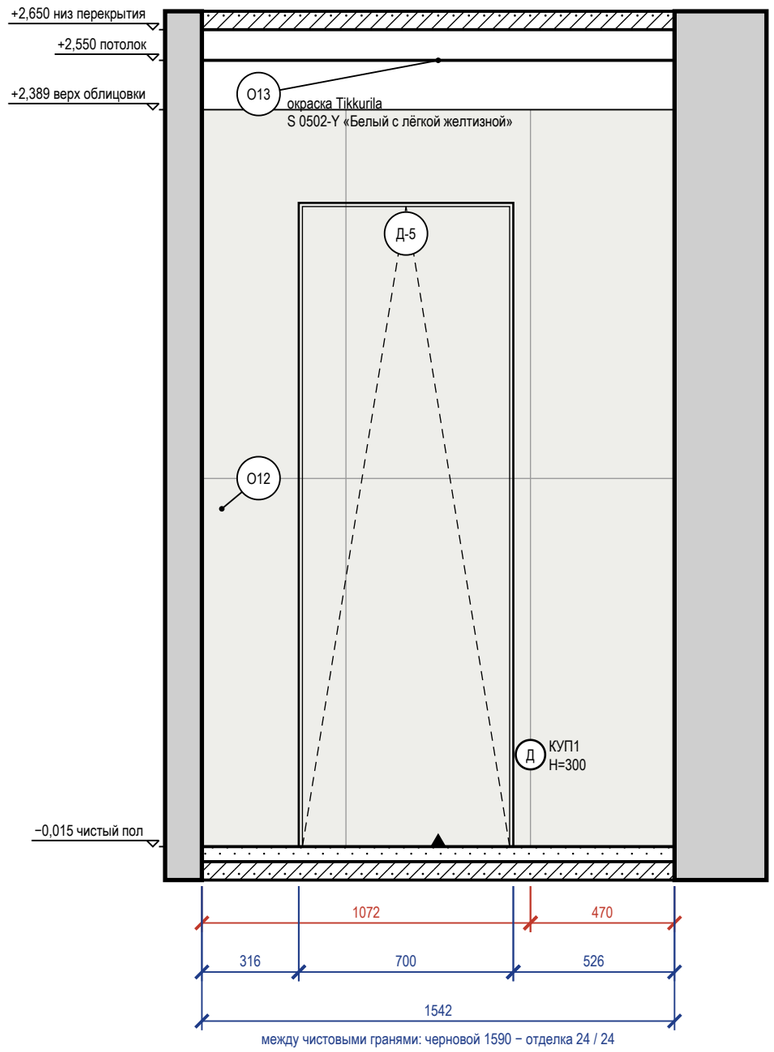


между чистовыми гранями: черновой 1590 − отделка 24 / 24

Развёртка стены Б

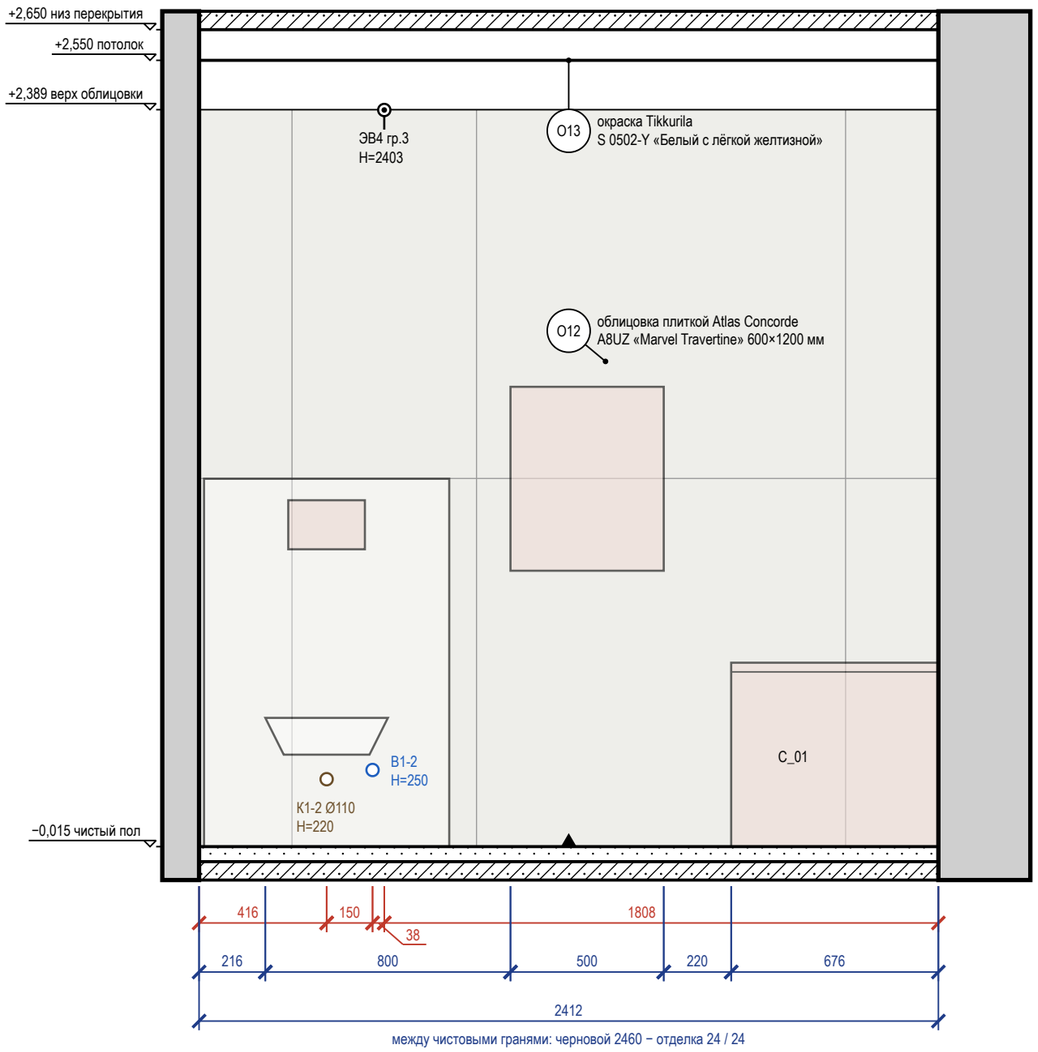

между чистовыми гранями: черновой 2460 − отделка 24 / 24

Схема развёрток (М 1:100)

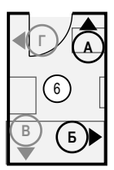

Ведомость отделки (на листе)


Марка	Поверхность	Материал, изделие	Цвет, код	Кол.
О12	стены	облицовка плиткой, Atlas Concorde Marvel Travertine, 600×1200×9 мм, A8UZ, затирка CG2WA	Atlas Concorde A8UZ «Marvel Travertine»	8 м²
О13	потолок	окраска, Tikkurila Luja 7, матовая, подготовка Q3	NCS S 0502-Y «Белый с лёгкой желтизной»	3,9 м²

Примечания

1. Размеры — в мм от чистовых поверхностей стен; условные обозначения и общие указания — лист 3.
2. Схема мебели, приборов и декора не является технической документацией для производства мебели; габариты — по паспортам изделий.
3. Выводы ВК — коды и высоты по листу выводов сантехники.
4. Облицовка — по сетке швов 2 мм, раскладка от оси стены (треугольник у пола), целые ряды от пола; подрезки — по листу раскладки плитки.
5. Гидроизоляция в 2 слоя, заход на стены 200 мм; над ванной — до 2000 и 300 мм за борт — до облицовки, с актом скрытых работ и тестом проливом (узел — на листе узлов).
6. Двери скрытого монтажа — полотно в плоскости стены, отделка стены по полотну, плинтус прерывается у короба (узел — на листе узлов).


					Проект: Квартира 103 м²	М 1:20
	Лист	№ док.	Подпись	Дата		
Дизайнер	Кырлан А.С.			04.11.26	Развёртки стен А, Б. Ванная (пом. 6)	Стадия: П; Лист: 63; Листов: 96

Развёртка стены В

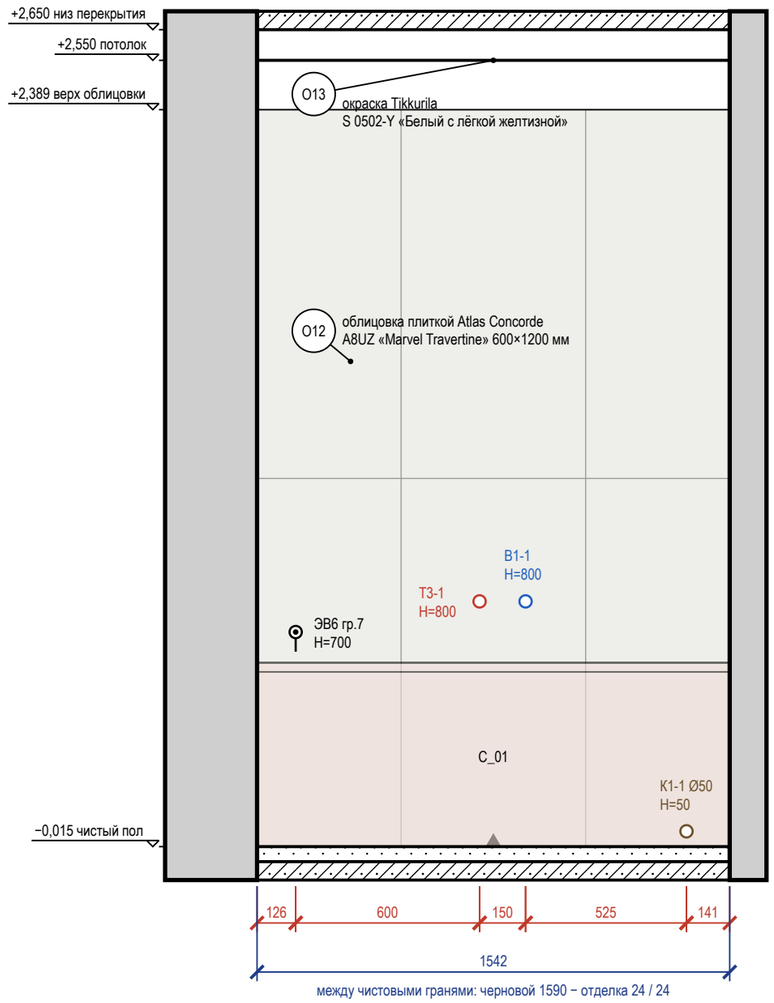


между чистовыми гранями: черновой 1590 − отделка 24 / 24

Развёртка стены Г

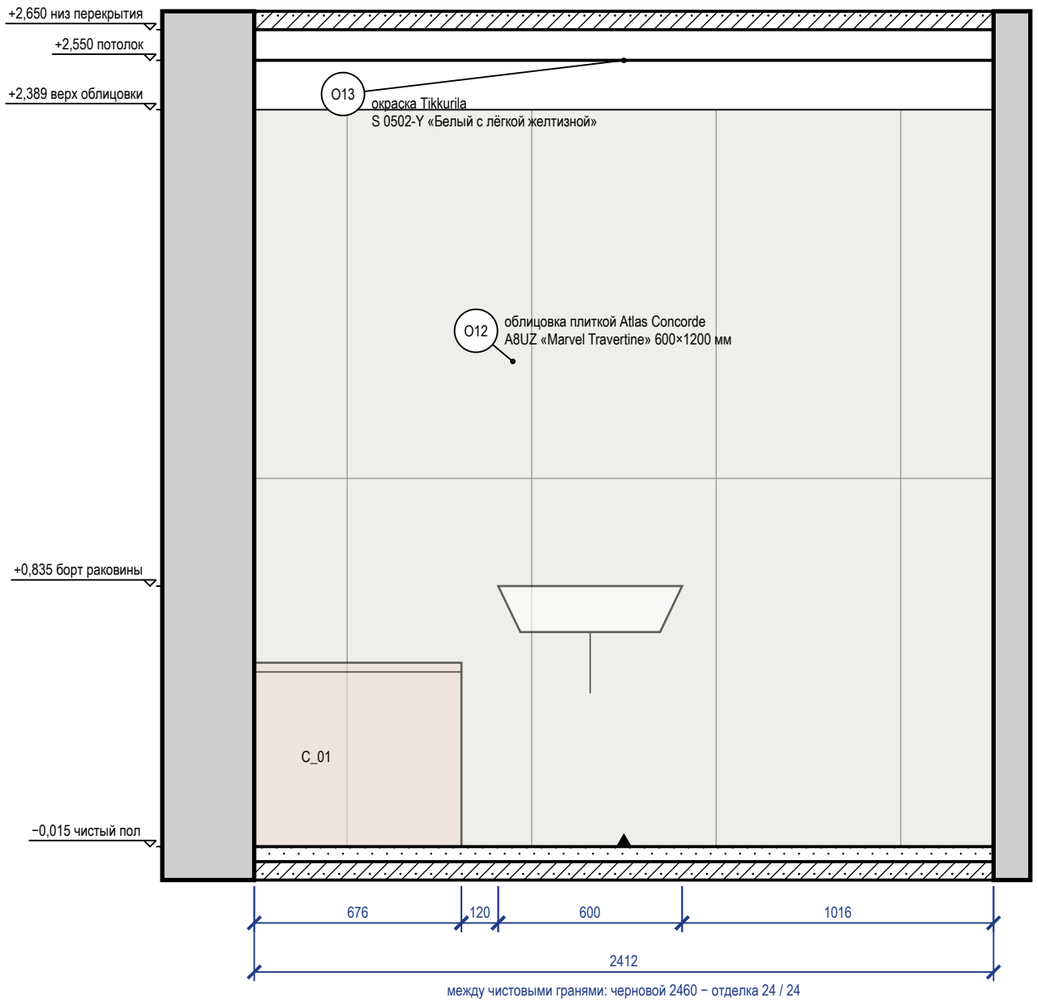

между чистовыми гранями: черновой 2460 − отделка 24 / 24

Схема развёрток (М 1:100)

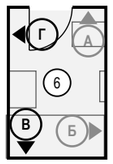

Ведомость отделки (на листе)

Марка	Поверхность	Материал, изделие	Цвет, код	Кол.
О12	стены	облицовка плиткой, Atlas Concorde Marvel Travertine, 600×1200×9 мм, A8UZ, затирка CG2WA	Atlas Concorde A8UZ «Marvel Travertine»	9,5 м²
О13	потолок	окраска, Tikkurila Luja 7, матовая, подготовка Q3	NCS S 0502-Y «Белый с лёгкой желтизной»	3,9 м²

Примечания

1. Размеры — в мм от чистовых поверхностей стен; условные обозначения и общие указания — лист 3.
2. Стена Г показана двумя видами: здесь — архитектурная развёртка (мебель, отделка, проёмы, высоты), электроточки и выводы ВК с привязками и таблицей — на листе 65 («Привязки»).
3. Схема мебели, приборов и декора не является технической документацией для производства мебели; габариты — по паспортам изделий.
4. Выводы ВК — коды и высоты по листу выводов сантехники.
5. Облицовка — по сетке швов 2 мм, раскладка от оси стены (треугольник у пола), целые ряды от пола; подрезки — по листу раскладки плитки.
6. Гидроизоляция в 2 слоя, заход на стены 200 мм; над ванной — до 2000 и 300 мм за борт — до облицовки, с актом скрытых работ и тестом проливом (узел — на листе узлов).

					Проект: Квартира 103 м²	М 1:20
	Лист	№ док.	Подпись	Дата		
Дизайнер	Кырлан А.С.			04.11.26	Развёртки стен В, Г. Ванная (пом. 6)	

Стадия	Лист	Листов
П	64	96

Развёртка стены Г: электроточки и выводы

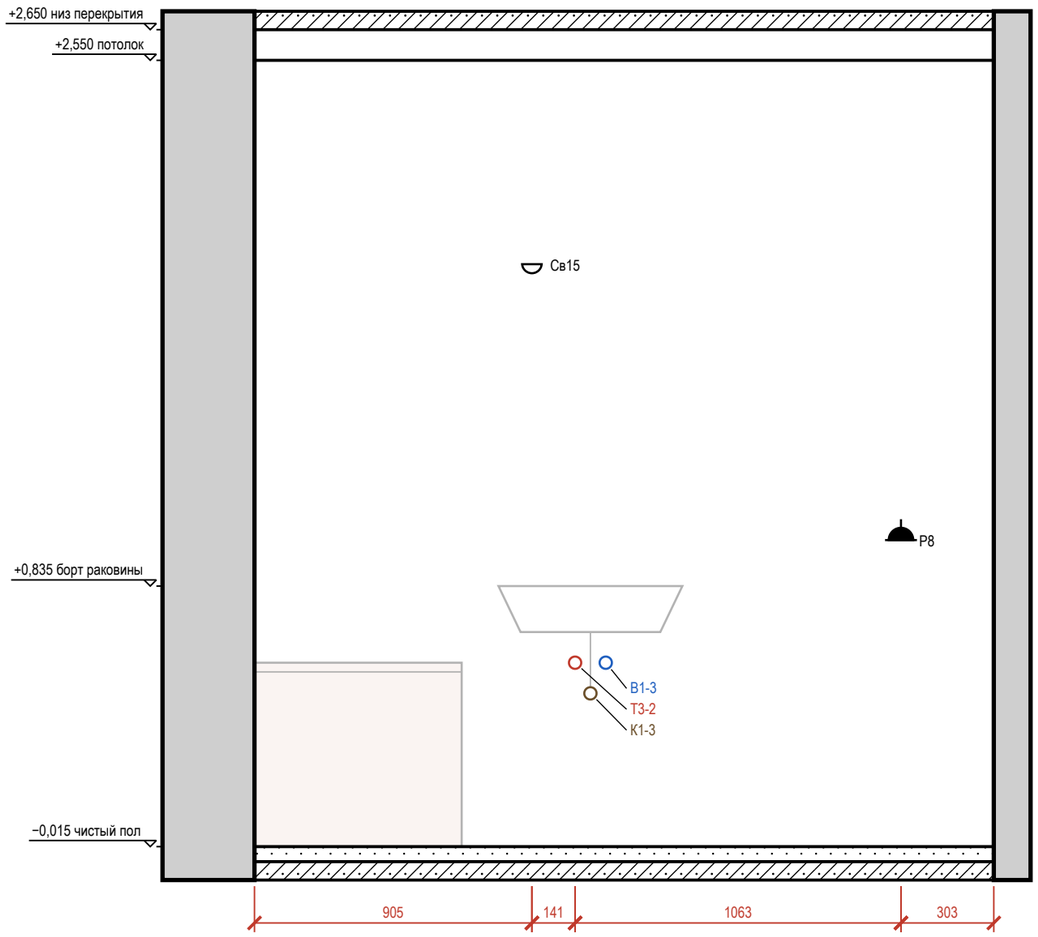


Таблица привязок электроточек и выводов

Марка	Назначение	От угла, мм	Н от пола, мм	Примечание
Св15	светильник настенный	905	1900	гр. 3
Т3-2	горячая вода — умывальник	1046	600	межос. 100
К1-3	канализация — умывальник	1096	500	Ø50
В1-3	холодная вода — умывальник	1146	600	межос. 100
Р8	розетка: фен у умывальника	2109	1000	гр. 7, IP44

Условные обозначения

- розетка влагозащищённая IP44
- светильник настенный (бра), Н — высота оси
- вывод В1 (код — в ведомости привязок)
- вывод Т3 (код — в ведомости привязок)
- вывод К1 (код — в ведомости привязок)
- привязки точек и выводов от угла и от пола, мм
- марка развёртки: буква стены, стрелка — взгляд


Схема развёрток (М 1:50)

Примечания

1. Вид «Привязки» стены Г — электроточки и выводы ВК; архитектурная развёртка (мебель, отделка, проёмы, высоты) — на листе 64. Мебель и приборы — подложкой для ориентира; их марки и обозначения мебели, проёмов и стен — там же.
2. Привязки — в мм: по горизонтали от левого чистового угла стены до оси изделия, Н — от чистого пола до оси; все точки — в таблице привязок. Красная цепочка — привязки по осям; точки ближе 120 мм одна к другой в цепочку не дробятся — их привязки только в таблице.
3. У знака — марка электроточки (Р — розетка, S — выключатель, Св — светильник, ЭВ — вывод кабеля); условные обозначения и общие указания — лист 3.
4. Коды выводов ВК: В1 — холодная вода, Т3 — горячая вода, К1 — канализация; номер после дефиса — номер вывода на листе выводов сантехники.


					Проект: Квартира 103 м²	М 1:20
	Лист	№ док.	Подпись	Дата		
Дизайнер	Кырлан А.С.			04.11.26	Привязки электроточек и выводов ВК, стена Г. Ванная (пом. 6)	Стадия: П; Лист: 65; Листов: 96

Развёртка стены А

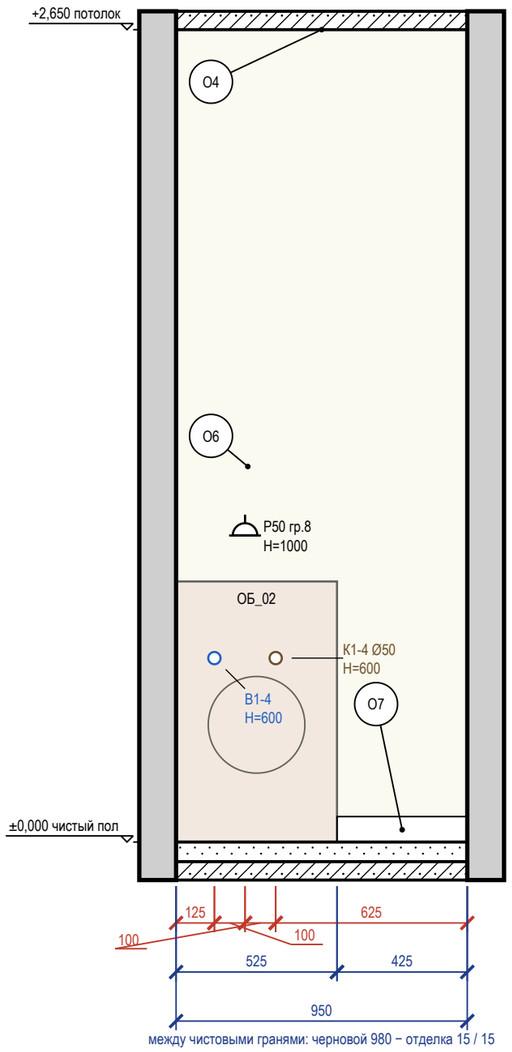


между чистовыми гранями: черновой 980 − отделка 15 / 15

Развёртка стены Б

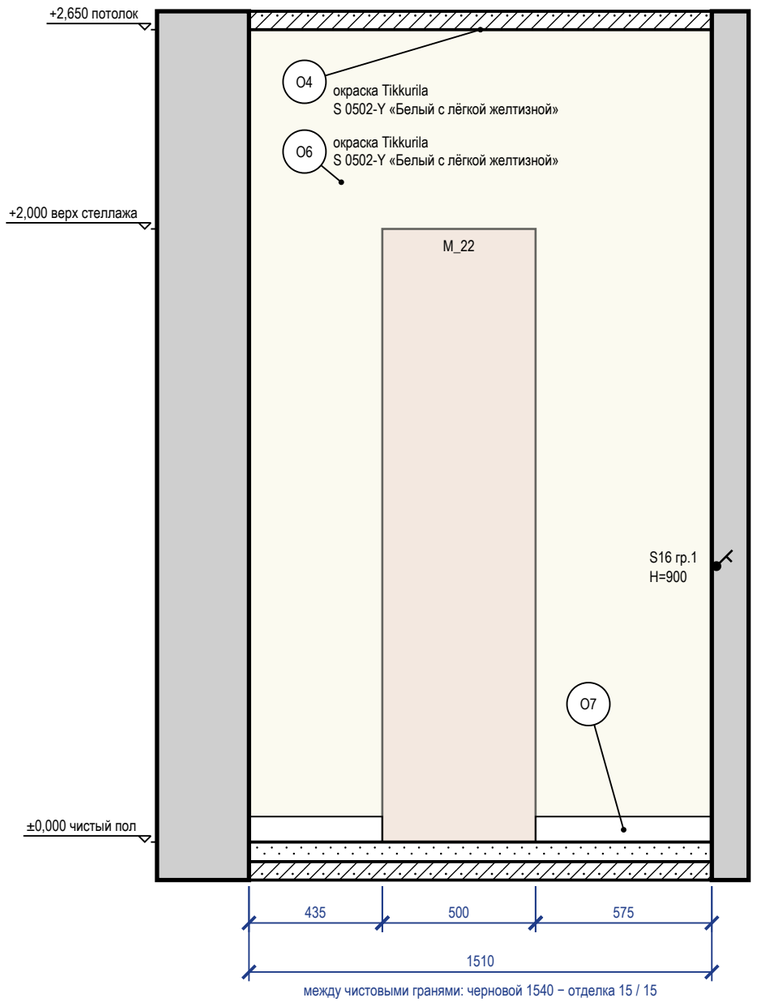


между чистовыми гранями: черновой 1540 − отделка 15 / 15

Развёртка стены В

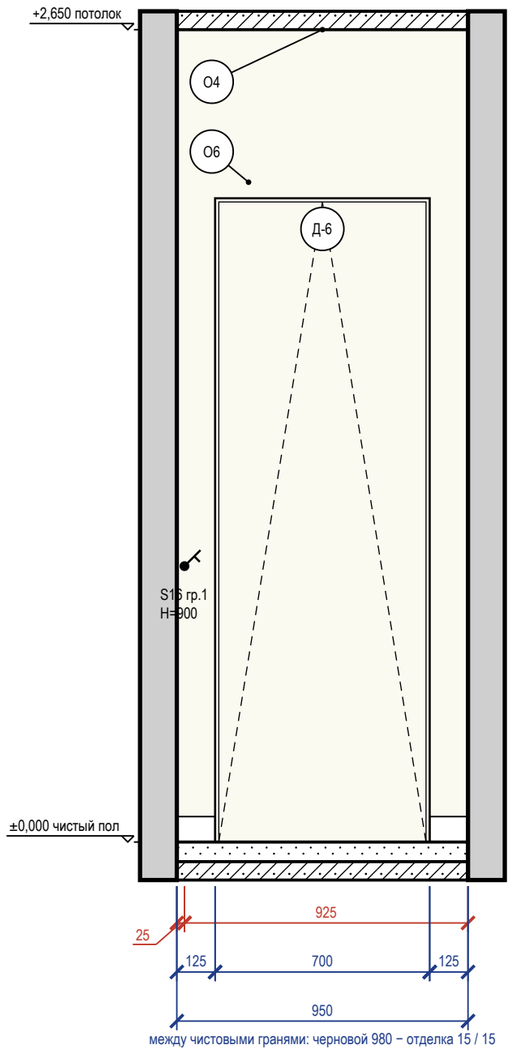

между чистовыми гранями: черновой 980 − отделка 15 / 15

Схема развёрток (М 1:100)

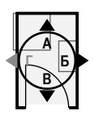

Ведомость отделки (на листе)

Марка	Поверхность	Материал, изделие	Цвет, код	Кол.
О4	потолок	окраска, Tikkurila Anti-Reflex 2, глубокоматовая, подготовка Q3	NCS S 0502-Y «Белый с лёгкой желтизной»	1,5 м²
О6	стены	окраска, Tikkurila Harmony, матовая, подготовка Q3	NCS S 0502-Y «Белый с лёгкой желтизной»	7,6 м²
О7	плинтус	плинтус МДФ, h 83 мм, Ultrawood Base 5340, ЛДФ под окраску, 83×15 мм, 2440 мм (арт. LDF-BASE-5340)	NCS S 0502-Y «Белый с лёгкой желтизной»	1,7 м

Примечания

1. Размеры — в мм от чистовых поверхностей стен; условные обозначения и общие указания — лист 3.
2. Схема мебели, приборов и декора не является технической документацией для производства мебели; габариты — по паспортам изделий.
3. Выводы ВК — коды и высоты по листу выводов сантехники.
4. Двери скрытого монтажа — полотно в плоскости стены, отделка стены по полотну, плинтус прерывается у короба (узел — на листе узлов).

					Проект: Квартира 103 м²	М 1:20
	Лист	№ док.	Подпись	Дата	Развёртки стен А, Б, В. Постирочная (пом. 7)	Стадия / Лист / Листов
Дизайнер	Кырлан А.С.			04.11.26		П / 66 / 96

Развёртка стены Г


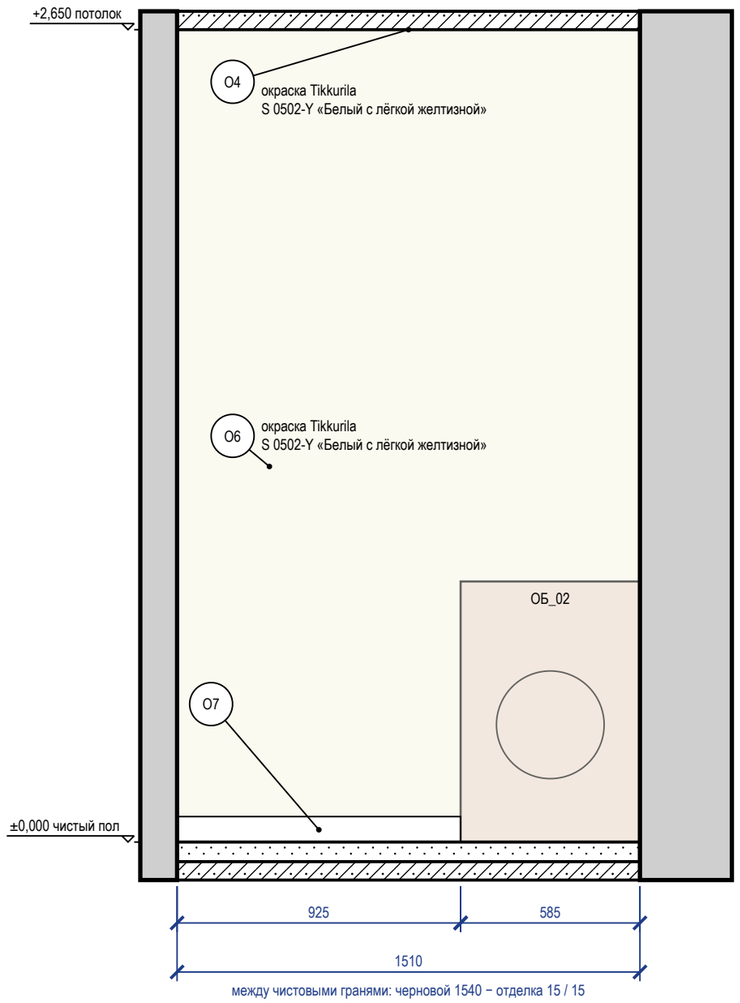


Схема развёрток (М 1:100)

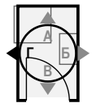

Ведомость отделки (на листе)


Марка	Поверхность	Материал, изделие	Цвет, код	Кол.
О4	потолок	окраска, Tikkurila Anti-Reflex 2, глубокоматовая, подготовка Q3	NCS S 0502-Y «Белый с лёгкой желтизной»	1,5 м²
О6	стены	окраска, Tikkurila Harmony, матовая, подготовка Q3	NCS S 0502-Y «Белый с лёгкой желтизной»	4 м²
О7	плинтус	плинтус МДФ, h 83 мм, Ultrawood Base 5340, ЛДФ под окраску, 83×15 мм, 2440 мм (арт. LDF-BASE-5340)	NCS S 0502-Y «Белый с лёгкой желтизной»	0,9 м

Примечания

1. Размеры — в мм от чистовых поверхностей стен; условные обозначения и общие указания — лист 3.
2. Схема мебели, приборов и декора не является технической документацией для производства мебели; габариты — по паспортам изделий.


					Проект: Квартира 103 м²	М 1:20
	Лист	№ док.	Подпись	Дата	Развёртка стены Г. Постирочная (пом. 7)	Стадия / Лист / Листов
Дизайнер	Кырлан А.С.			04.11.26		П / 67 / 96

Развёртка стены А

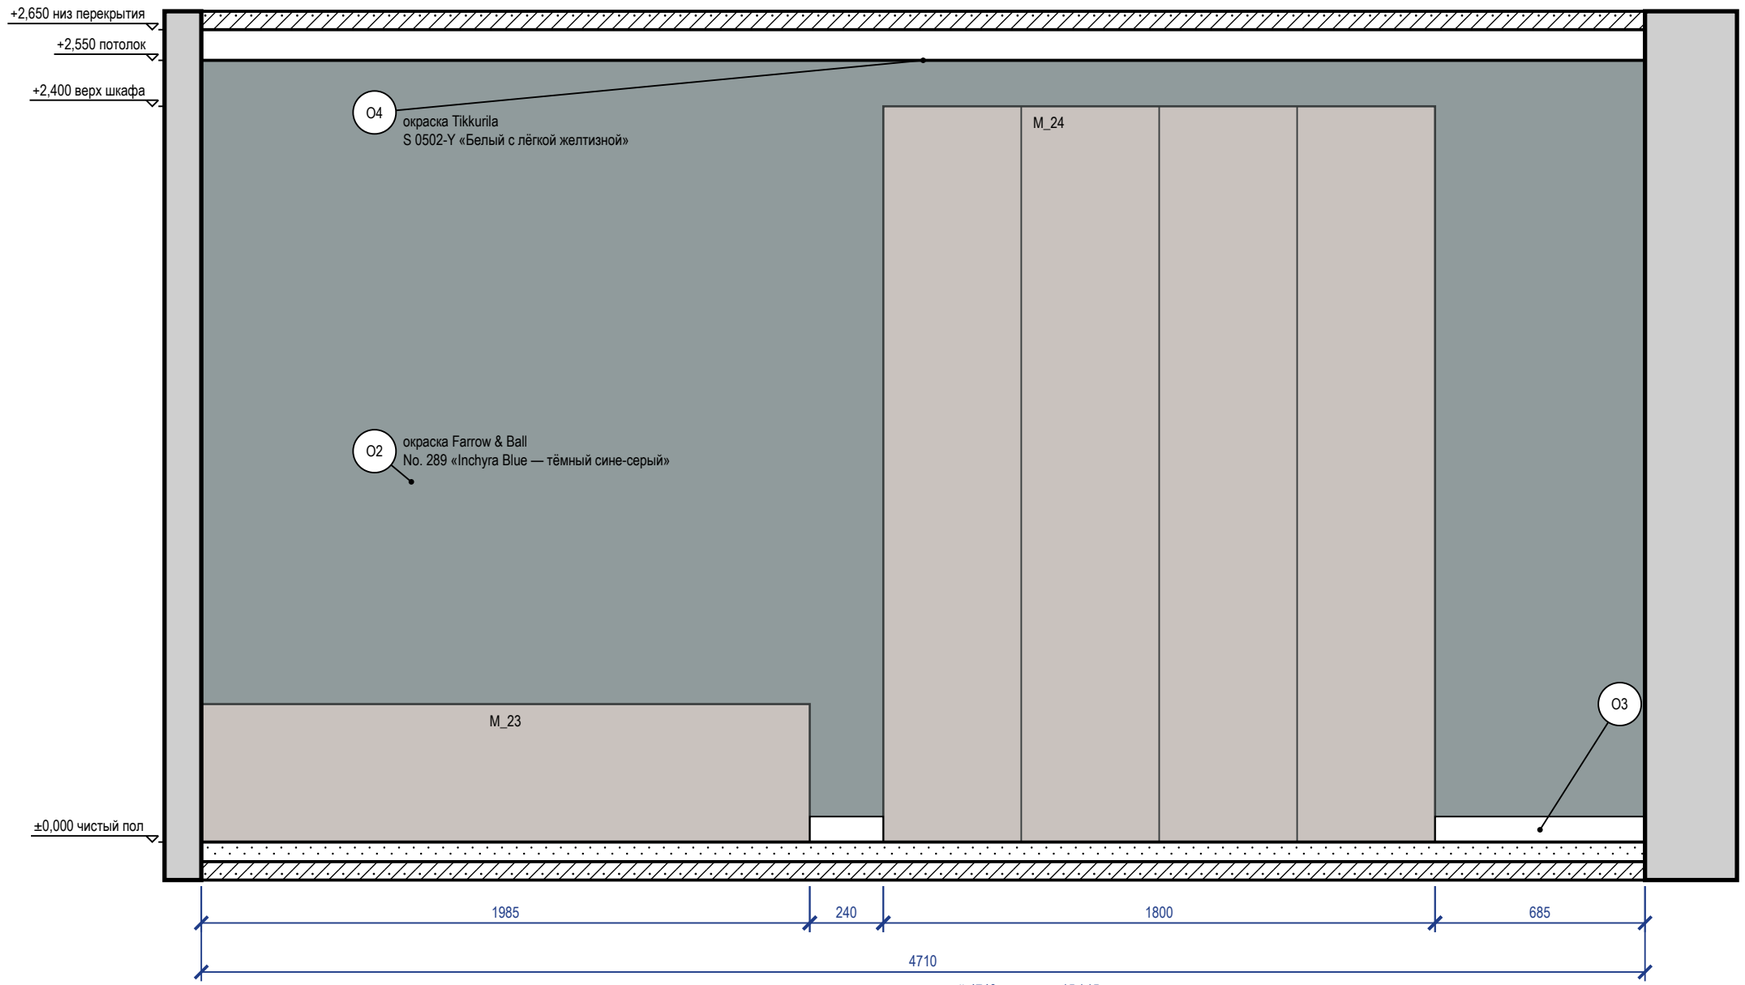

между чистовыми гранями: черновой 4740 − отделка 15 / 15

Схема развёрток (М 1:100)

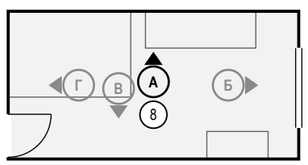

Ведомость отделки (на листе)

Марка	Поверхность	Материал, изделие	Цвет, код	Кол.
O2	акцентная стена	окраска, Farrow & Ball Modern Emulsion, матовая, подготовка Q3	Farrow & Ball No. 289 «Inchyra Blue — тёмный сине-серый»	12 м²
O3	плинтус	плинтус МДФ, h 83 мм, Ultrawood Base 5340, ЛДФ под окраску, 83×15 мм, 2440 мм (арт. LDF-BASE-5340)	Farrow & Ball No. 291 «School House White тёплый меловой белый»	0,9 м
O4	потолок	окраска, Tikkurila Anti-Reflex 2, глубокоматовая, подготовка Q3	NCS S 0502-Y «Белый с лёгкой желтизной»	11,4 м²


Примечания

1. Размеры — в мм от чистовых поверхностей стен; условные обозначения и общие указания — лист 3.

					Проект: Квартира 103 м²	М 1:20
	Лист	№ док.	Подпись	Дата		
Дизайнер	Кырлан А.С.			04.11.26	Развёртка стены А. Спальня 2 (пом. 8)	Стадия: П; Лист: 68; Листов: 96


выпуск 04.11.2026 № d6a6e5e88d · стр. 68 из 96

Развёртка стены Б

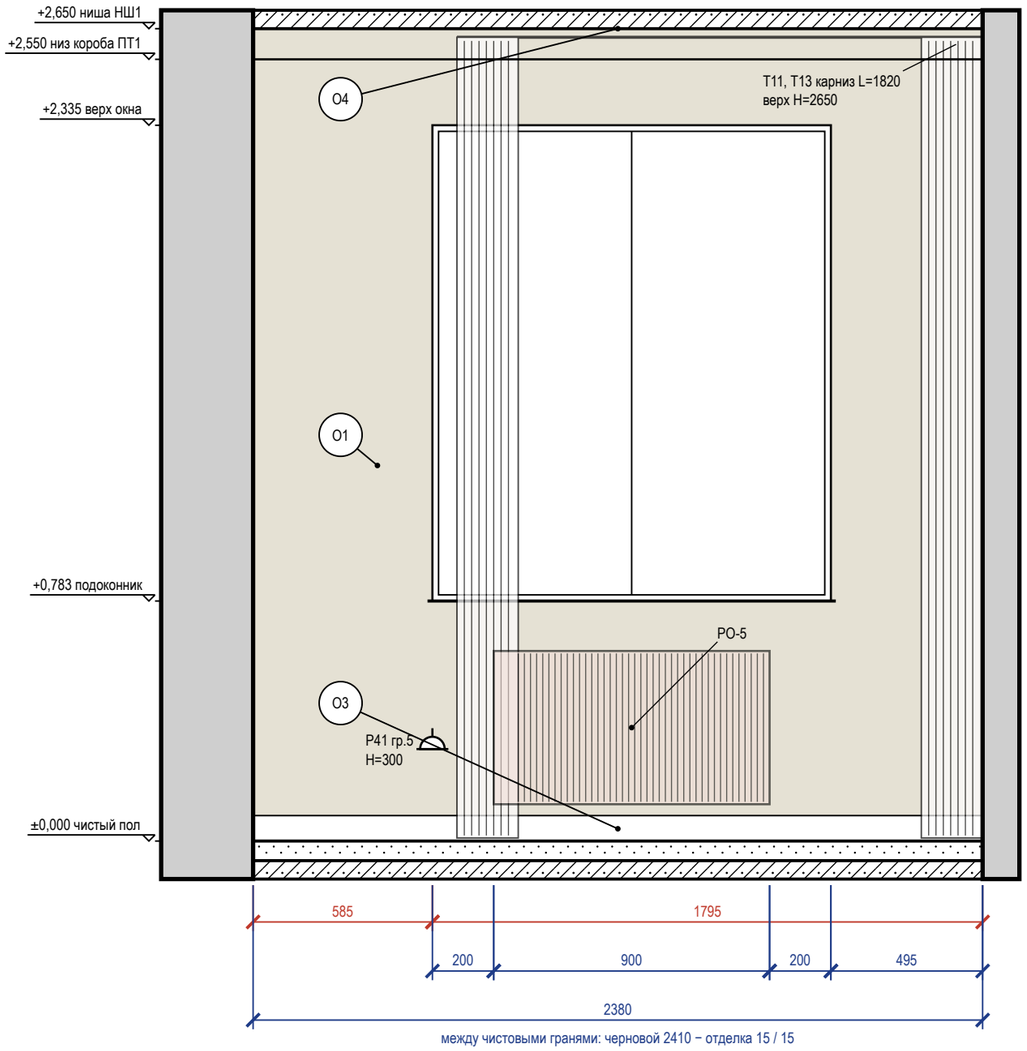


между чистовыми гранями: черновой 2410 − отделка 15 / 15

Развёртка стены Г

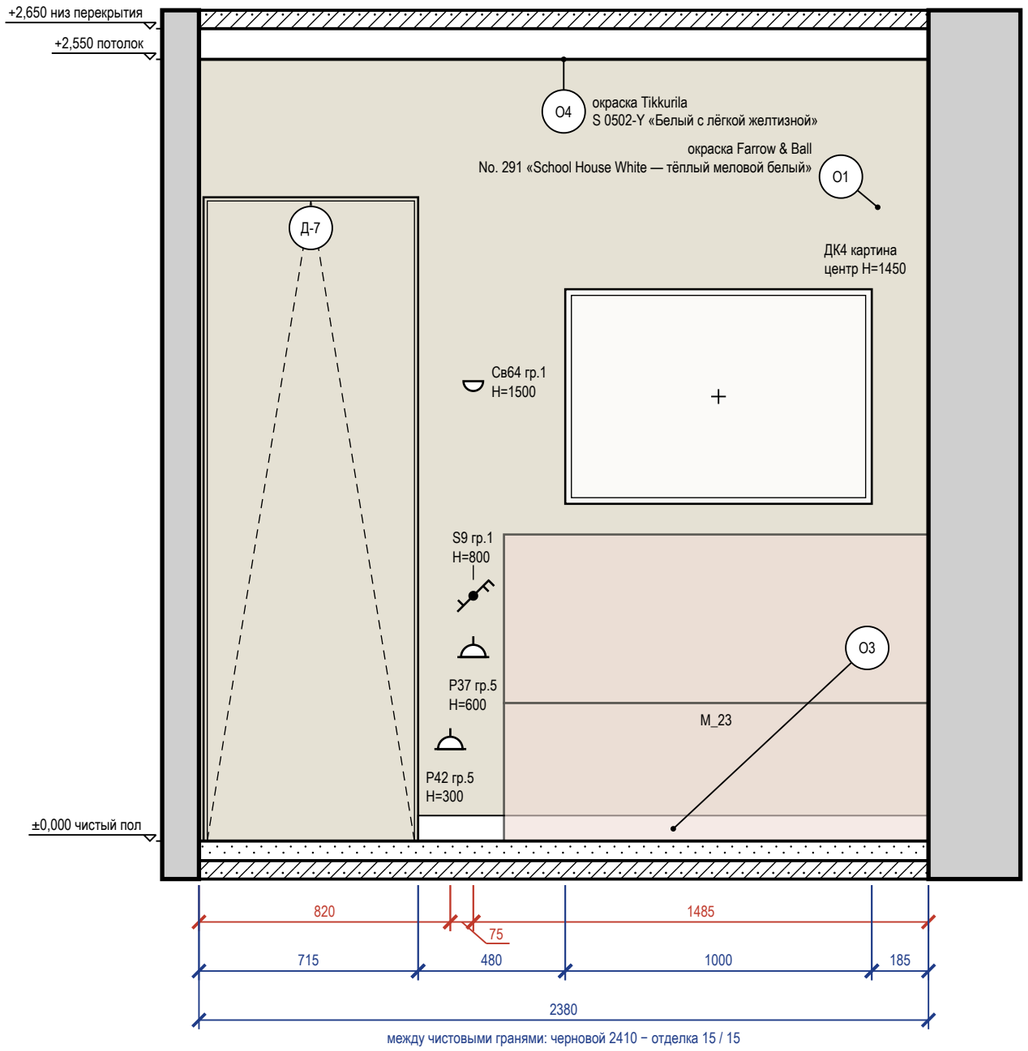

между чистовыми гранями: черновой 2410 − отделка 15 / 15

Схема развёрток (М 1:100)

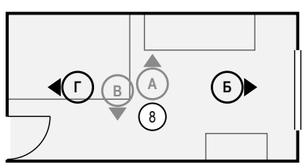

Ведомость отделки (на листе)

Марка	Поверхность	Материал, изделие	Цвет, код	Кол.
О1	стены	окраска, Farrow & Ball Modern Emulsion, матовая, подготовка Q3	Farrow & Ball No. 291 «School House White тёплый меловой белый»	8,9 м²
О3	плинтус	плинтус МДФ, h 83 мм, Ultrawood Base 5340, ЛДФ под окраску, 83×15 мм, 2440 мм (арт. LDF-BASE-5340)	Farrow & Ball No. 291 «School House White тёплый меловой белый»	4 м
О4	потолок	окраска, Tikkurila Anti-Reflex 2, глубокоматовая, подготовка Q3	NCS S 0502-Y «Белый с лёгкой желтизной»	11,4 м²

Примечания

1. Размеры — в мм от чистовых поверхностей стен; условные обозначения и общие указания — лист 3.
2. Картины и зеркала крепить к основанию по паспорту изделия (закладные и анкеры — в перечне скрытых работ); крест — ось центра предмета.
3. Карнизы (шины) — по ведомости текстиля декоратора: длина L и верх Н на развёртке — те же числа, что в ведомости; крепление — до окраски потолка.
4. Двери скрытого монтажа — полотно в плоскости стены, отделка стены по полотну, плинтус прерывается у короба (узел — на листе узлов).
5. Карниз Т11, Т13: по ведомости текстиля шина L=1820 мм, а от её начала до чистового угла стены — 1715 мм: шина не встаёт, длину согласовать с декоратором до заказа.
6. Линии узора (швы плитки, складки штор, рёбра радиаторов) прерываются у знаков и выносок — просвет между линиями не менее 0,7 мм.

					Проект: Квартира 103 м²	М 1:20
	Лист	№ док.	Подпись	Дата		
Дизайнер	Кырлан А.С.			04.11.26	Развёртки стен Б, Г. Спальня 2 (пом. 8)	Стадия: П; Лист: 69; Листов: 96

Развёртка стены В


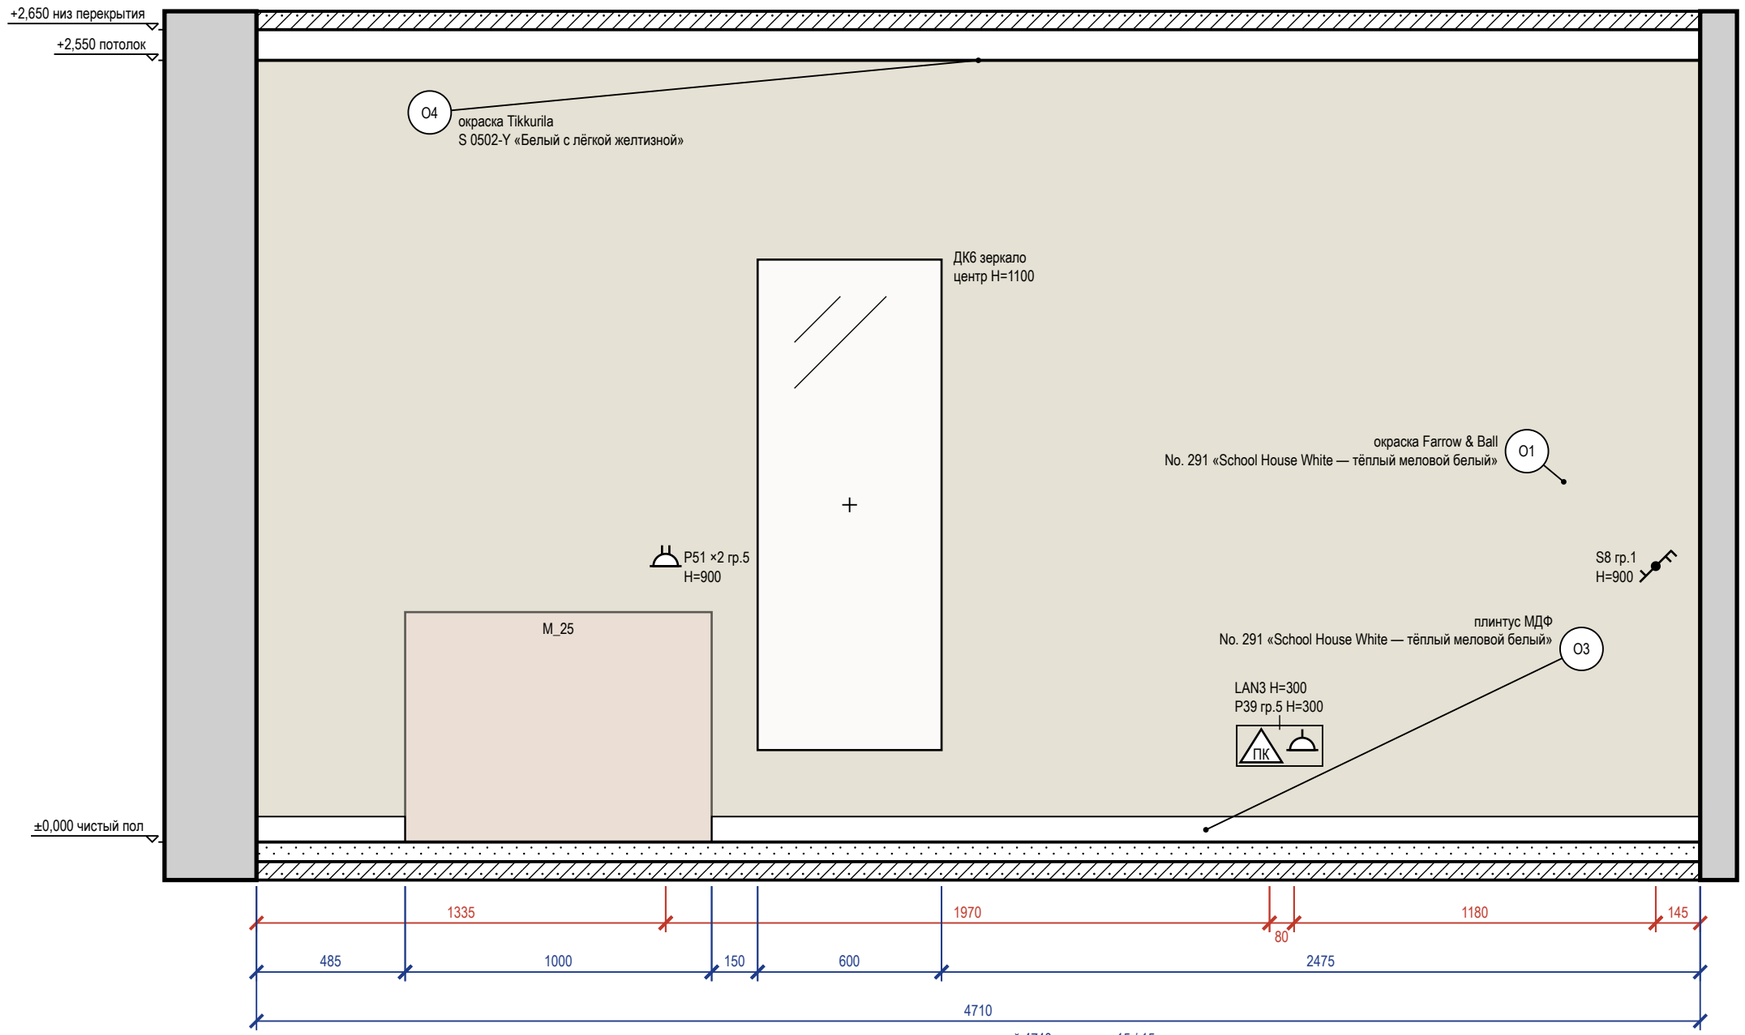


Схема развёрток (М 1:100)

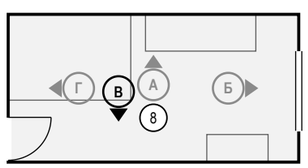

Ведомость отделки (на листе)

Марка	Поверхность	Материал, изделие	Цвет, код	Кол.
О1	стены	окраска, Farrow & Ball Modern Emulsion, матовая, подготовка Q3	Farrow & Ball No. 291 «School House White тёплый меловой белый»	12 м²
О3	плинтус	плинтус МДФ, h 83 мм, Ultrawood Base 5340, ЛДФ под окраску, 83×15 мм, 2440 мм (арт. LDF-BASE-5340)	Farrow & Ball No. 291 «School House White тёплый меловой белый»	3,7 м
О4	потолок	окраска, Tikkurila Anti-Reflex 2, глубокоматовая, подготовка Q3	NCS S 0502-Y «Белый с лёгкой желтизной»	11,4 м²

Примечания

1. Размеры — в мм от чистовых поверхностей стен; условные обозначения и общие указания — лист 3.
2. Картины и зеркала крепить к основанию по паспорту изделия (закладные и анкеры — в перечне скрытых работ); крест — ось центра предмета.

	Лист	№ док.	Подпись	Дата
Дизайнер	Кырлан А.С.			04.11.26

Проект: Квартира 103 м² — **М 1:20**

Развёртка стены В. Спальня 2 (пом. 8)

Стадия	Лист	Листов
П	70	96

выпуск 04.11.2026 № d6a6e5e88d · стр. 70 из 96

Развёртка стены А

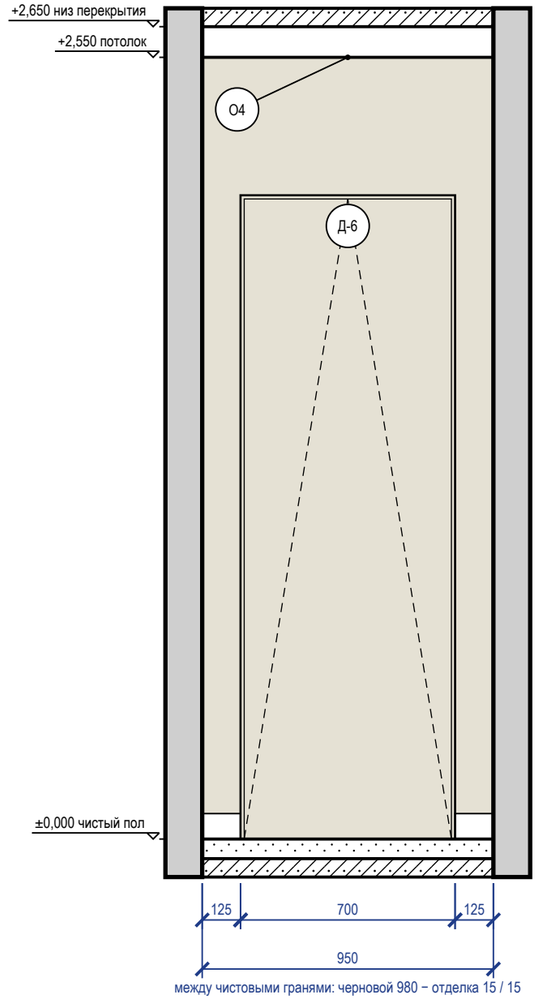


Схема развёрток (М 1:100)



Ведомость отделки (на листе)

Марка	Поверхность	Материал, изделие	Цвет, код	Кол.
О1	стены	окраска, Farrow & Ball Modern Emulsion, матовая, подготовка Q3	Farrow & Ball No. 291 «School House White — тёплый меловой белый»	1 м²
О3	плинтус	плинтус МДФ, h 83 мм, Ultrawood Base 5340, ЛДФ под окраску, 83×15 мм, 2440 мм (арт. LDF-BASE-5340)	Farrow & Ball No. 291 «School House White — тёплый меловой белый»	0,3 м
О4	потолок	окраска, Tikkurila Anti-Reflex 2, глубокоматовая, подготовка Q3	NCS S 0502-Y «Белый с лёгкой желтизной»	6 м²

Примечания

1. Размеры — в мм от чистовых поверхностей стен; условные обозначения и общие указания — лист 3.
2. Двери скрытого монтажа — полотно в плоскости стены, отделка стены по полотну, плинтус прерывается у короба (узел — на листе узлов).

	Лист	№ док.	Подпись	Дата
Дизайнер	Кырлан А.С.			04.11.26

Проект: Квартира 103 м² — **М 1:20**

Развёртка стены А. Коридор (пом. 9)

Стадия	Лист	Листов
П	71	96

Развёртка стены Б


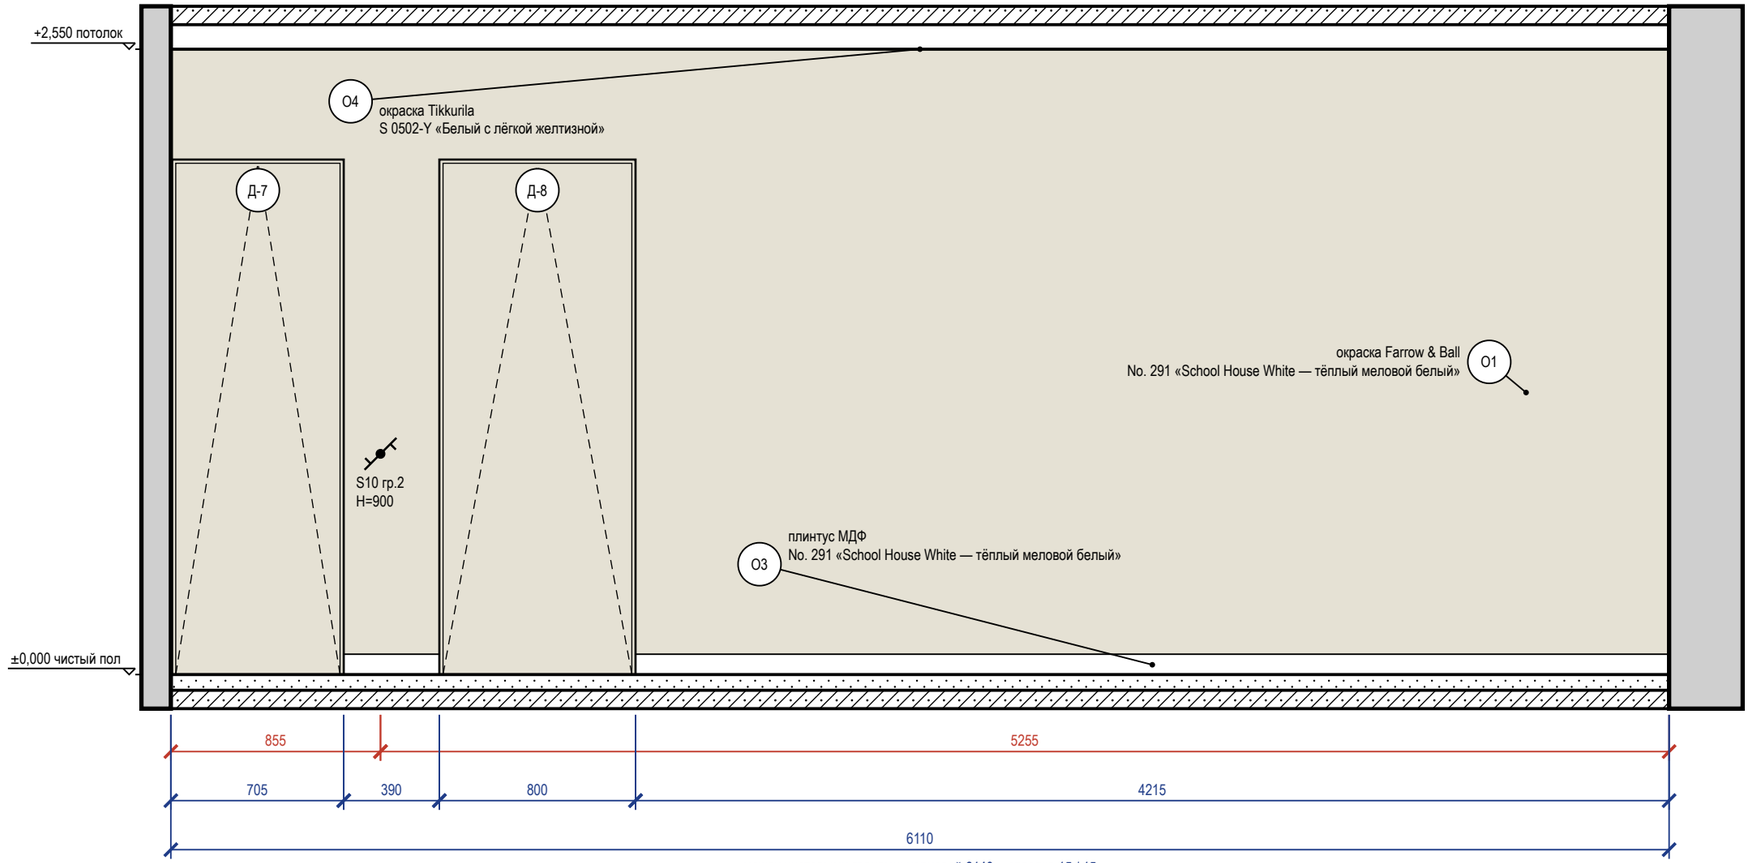


Схема развёрток (М 1:100)

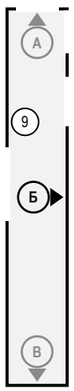

Ведомость отделки (на листе)

Марка	Поверхность	Материал, изделие	Цвет, код	Кол.
О1	стены	окраска, Farrow & Ball Modern Emulsion, матовая, подготовка Q3	Farrow & Ball No. 291 «School House White тёплый меловой белый»	12,4 м²
О3	плинтус	плинтус МДФ, h 83 мм, Ultrawood Base 5340, ЛДФ под окраску, 83×15 мм, 2440 мм (арт. LDF-BASE-5340)	Farrow & Ball No. 291 «School House White тёплый меловой белый»	4,6 м
О4	потолок	окраска, Tikkurila Anti-Reflex 2, глубокоматовая, подготовка Q3	NCS S 0502-Y «Белый с лёгкой желтизной»	6 м²

Примечания

1. Размеры — в мм от чистовых поверхностей стен; условные обозначения и общие указания — лист 3.
2. Двери скрытого монтажа — полотно в плоскости стены, отделка стены по полотну, плинтус прерывается у короба (узел — на листе узлов).

	Лист	№ док.	Подпись	Дата
Дизайнер	Кырлан А.С.			04.11.26

Проект: Квартира 103 м² — **М 1:25**

Развёртка стены Б. Коридор (пом. 9)

Стадия	Лист	Листов
П	72	96

Развёртка стены В

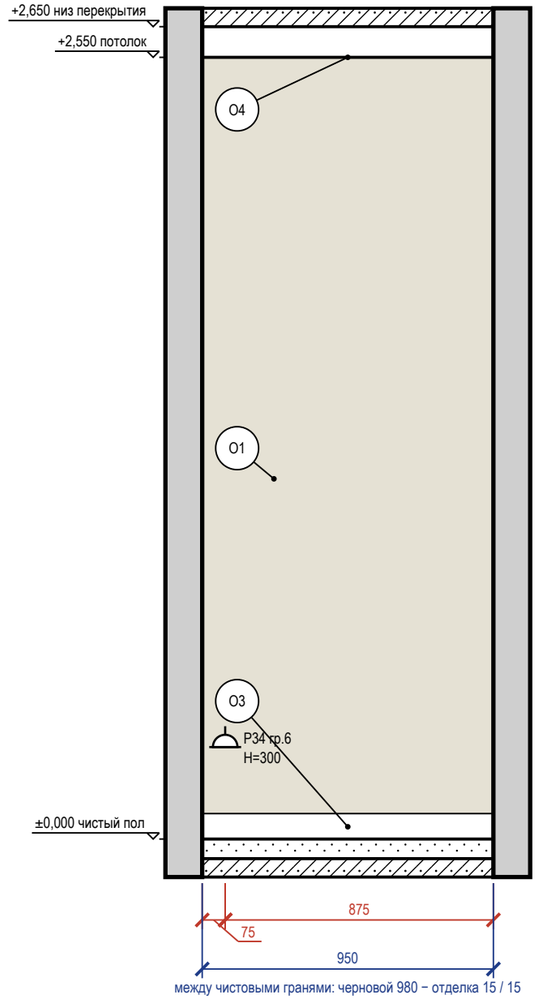


Схема развёрток (М 1:100)



Ведомость отделки (на листе)

Марка	Поверхность	Материал, изделие	Цвет, код	Кол.
О1	стены	окраска, Farrow & Ball Modern Emulsion, матовая, подготовка Q3	Farrow & Ball No. 291 «School House White — тёплый меловой белый»	2,4 м²
О3	плинтус	плинтус МДФ, h 83 мм, Ultrawood Base 5340, ЛДФ под окраску, 83×15 мм, 2440 мм (арт. LDF-BASE-5340)	Farrow & Ball No. 291 «School House White — тёплый меловой белый»	0,9 м
О4	потолок	окраска, Tikkurila Anti-Reflex 2, глубокоматовая, подготовка Q3	NCS S 0502-Y «Белый с лёгкой желтизной»	6 м²

Примечания

1. Размеры — в мм от чистовых поверхностей стен; условные обозначения и общие указания — лист 3.

					Проект: Квартира 103 м²	М 1:20
	Лист	№ док.	Подпись	Дата		
Дизайнер	Кырлан А.С.			04.11.26	Развёртка стены В. Коридор (пом. 9)	
					Стадия: П	Лист: 73 / Листов: 96

Развёртка стены А


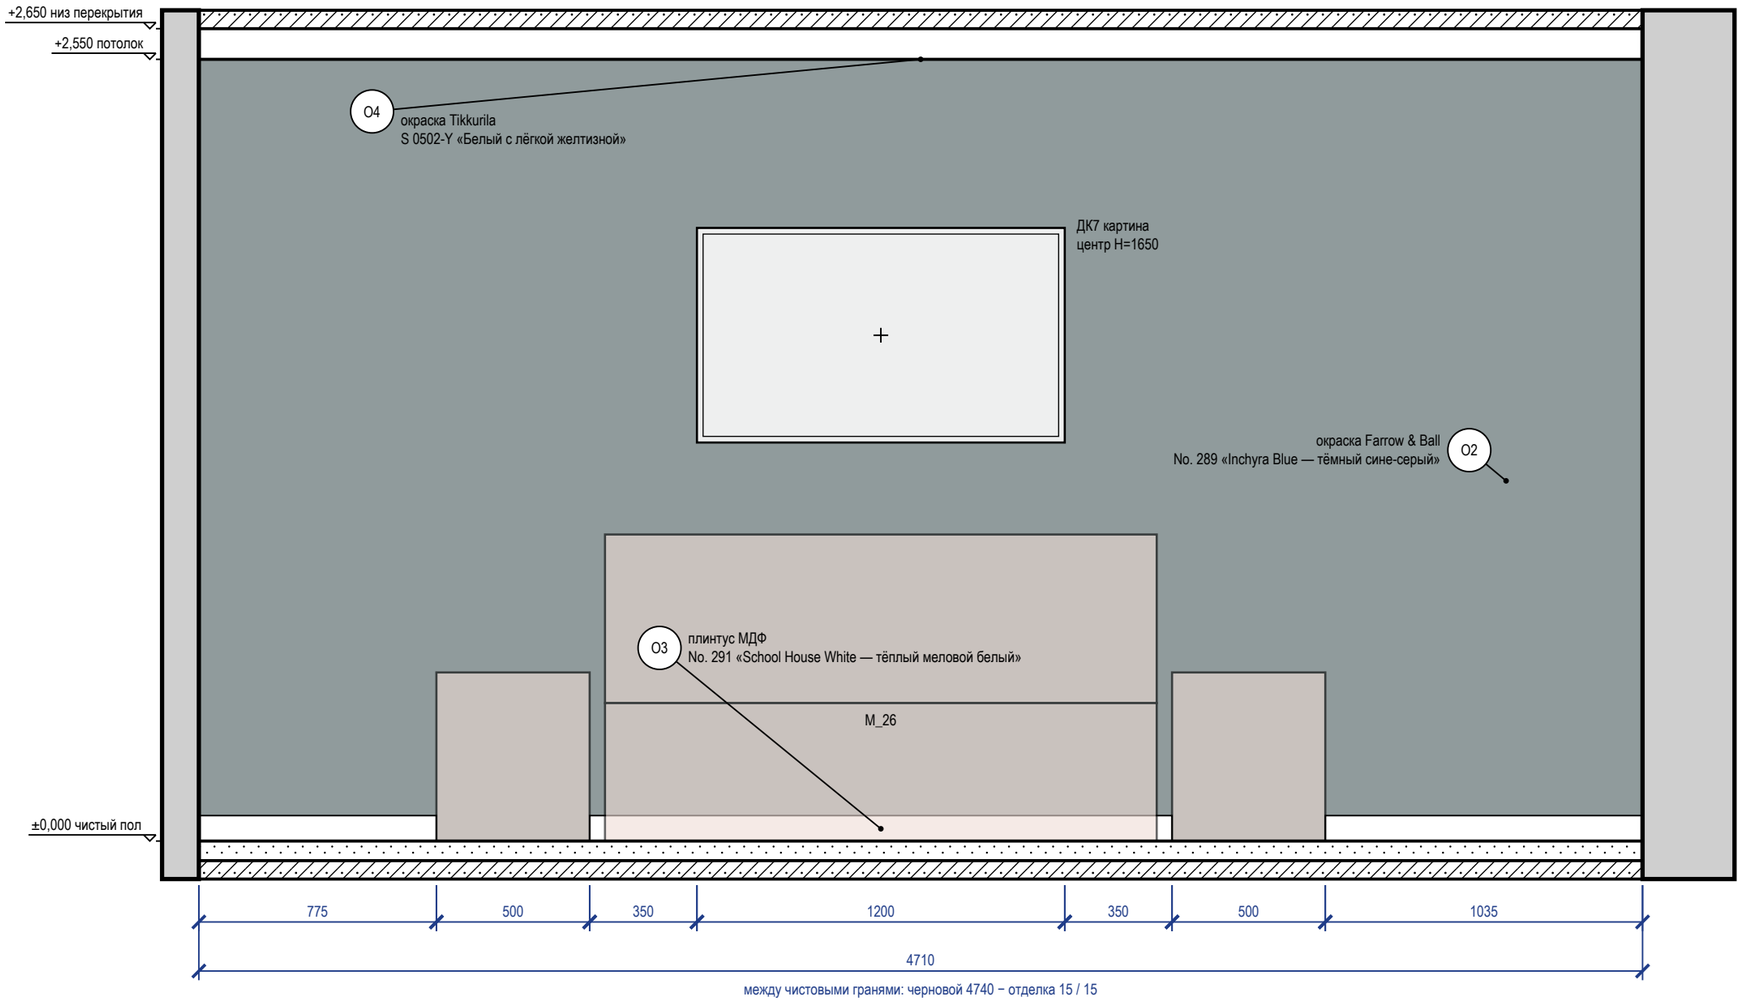


Схема развёрток (М 1:100)

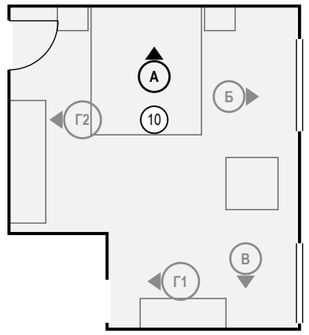

Ведомость отделки (на листе)

Марка	Поверхность	Материал, изделие	Цвет, код	Кол.
О2	акцентная стена	окраска, Farrow & Ball Modern Emulsion, матовая, подготовка Q3	Farrow & Ball No. 289 «Inchyra Blue — тёмный сине-серый»	12 м²
О3	плинтус	плинтус МДФ, h 83 мм, Ultrawood Base 5340, ЛДФ под окраску, 83×15 мм, 2440 мм (арт. LDF-BASE-5340)	Farrow & Ball No. 291 «School House White тёплый меловой белый»	3,7 м
О4	потолок	окраска, Tikkurila Anti-Reflex 2, глубокоматовая, подготовка Q3	NCS S 0502-Y «Белый с лёгкой желтизной»	22,5 м²

Примечания

1. Размеры — в мм от чистовых поверхностей стен; условные обозначения и общие указания — лист 3.
2. Стена А показана двумя видами: здесь — архитектурная развёртка (мебель, отделка, проёмы, высоты), электроточки и выводы ВК с привязками и таблицей — на листе 75 («Привязки»).
3. Картины и зеркала крепить к основанию по паспорту изделия (закладные и анкеры — в перечне скрытых работ); крест — ось центра предмета.

					Проект: Квартира 103 м² — М 1:20
	Лист	№ док.	Подпись	Дата	
Дизайнер	Кырлан А.С.			04.11.26	Развёртка стены А. Спальня мастер (пом. 10)
					Стадия: П; Лист: 74; Листов: 96

Развёртка стены А: электроточки и выводы

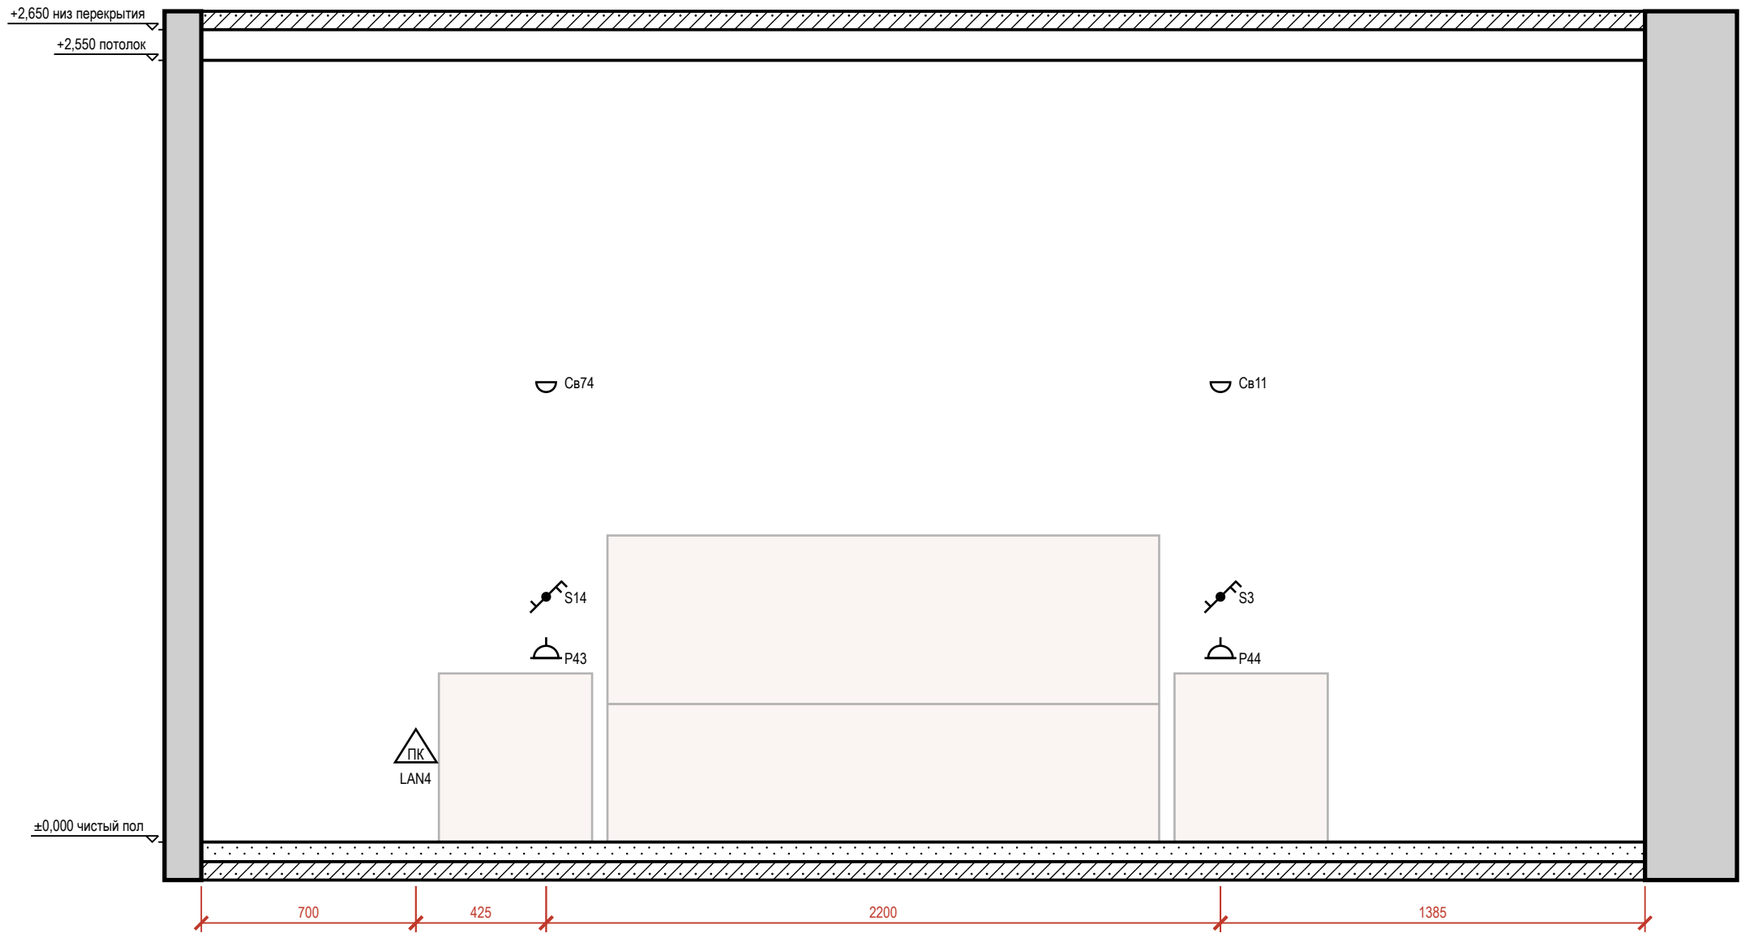



Таблица привязок электроточек и выводов

Марка	Назначение	От угла, мм	Н от пола, мм	Примечание
LAN4	розетка RJ45: передача данных	700	300	
P43	розетка: у кровати	1125	600	гр. 4
S14	выключатель	1125	800	гр. 1
Св74	светильник настенный	1125	1500	гр. 1
P44	розетка: у кровати	3325	600	гр. 4
S3	выключатель	3325	800	гр. 1
Св11	светильник настенный	3325	1500	гр. 1

Условные обозначения

- розетка с заземляющим контактом; у знака — марка, ×N постов в рамке, гр. — группа щита, Н — высота оси, мм
- выключатель одноклавишный
- выключатель двухклавишный (флажков — по числу клавиш)
- выключатель с проходной или перекрёстной клавишей (обратный флажок); тип клавиши — в подписи
- светильник настенный (бра), Н — высота оси
- ПК — розетка компьютерная RJ45
- привязки точек и выводов от угла и от пола, мм
- A — марка развёртки: буква стены, стрелка — взгляд

Схема развёрток (М 1:200)

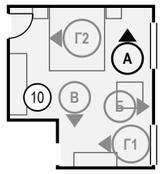

Примечания

1. Вид «Привязки» стены А — электроточки и выводы ВК; архитектурная развёртка (мебель, отделка, проёмы, высоты) — на листе 74. Мебель и приборы — подложкой для ориентира; их марки и обозначения мебели, проёмов и стен — там же.
2. Привязки — в мм: по горизонтали от левого чистового угла стены до оси изделия, Н — от чистого пола до оси; все точки — в таблице привязок. Красная цепочка — привязки по осям; точки ближе 120 мм одна к другой в цепочку не дробятся — их привязки только в таблице.
3. У знака — марка электроточки (Р — розетка, S — выключатель, Св — светильник, ЭВ — вывод кабеля); условные обозначения и общие указания — лист 3.

					Проект: Квартира 103 м² — М 1:20
	Лист	№ док.	Подпись	Дата	
Дизайнер	Кырлан А.С.			04.11.26	Привязки электроточек, стена А. Спальня мастер (пом. 10)

Стадия	Лист	Листов
П	75	96

Развёртка стены Б


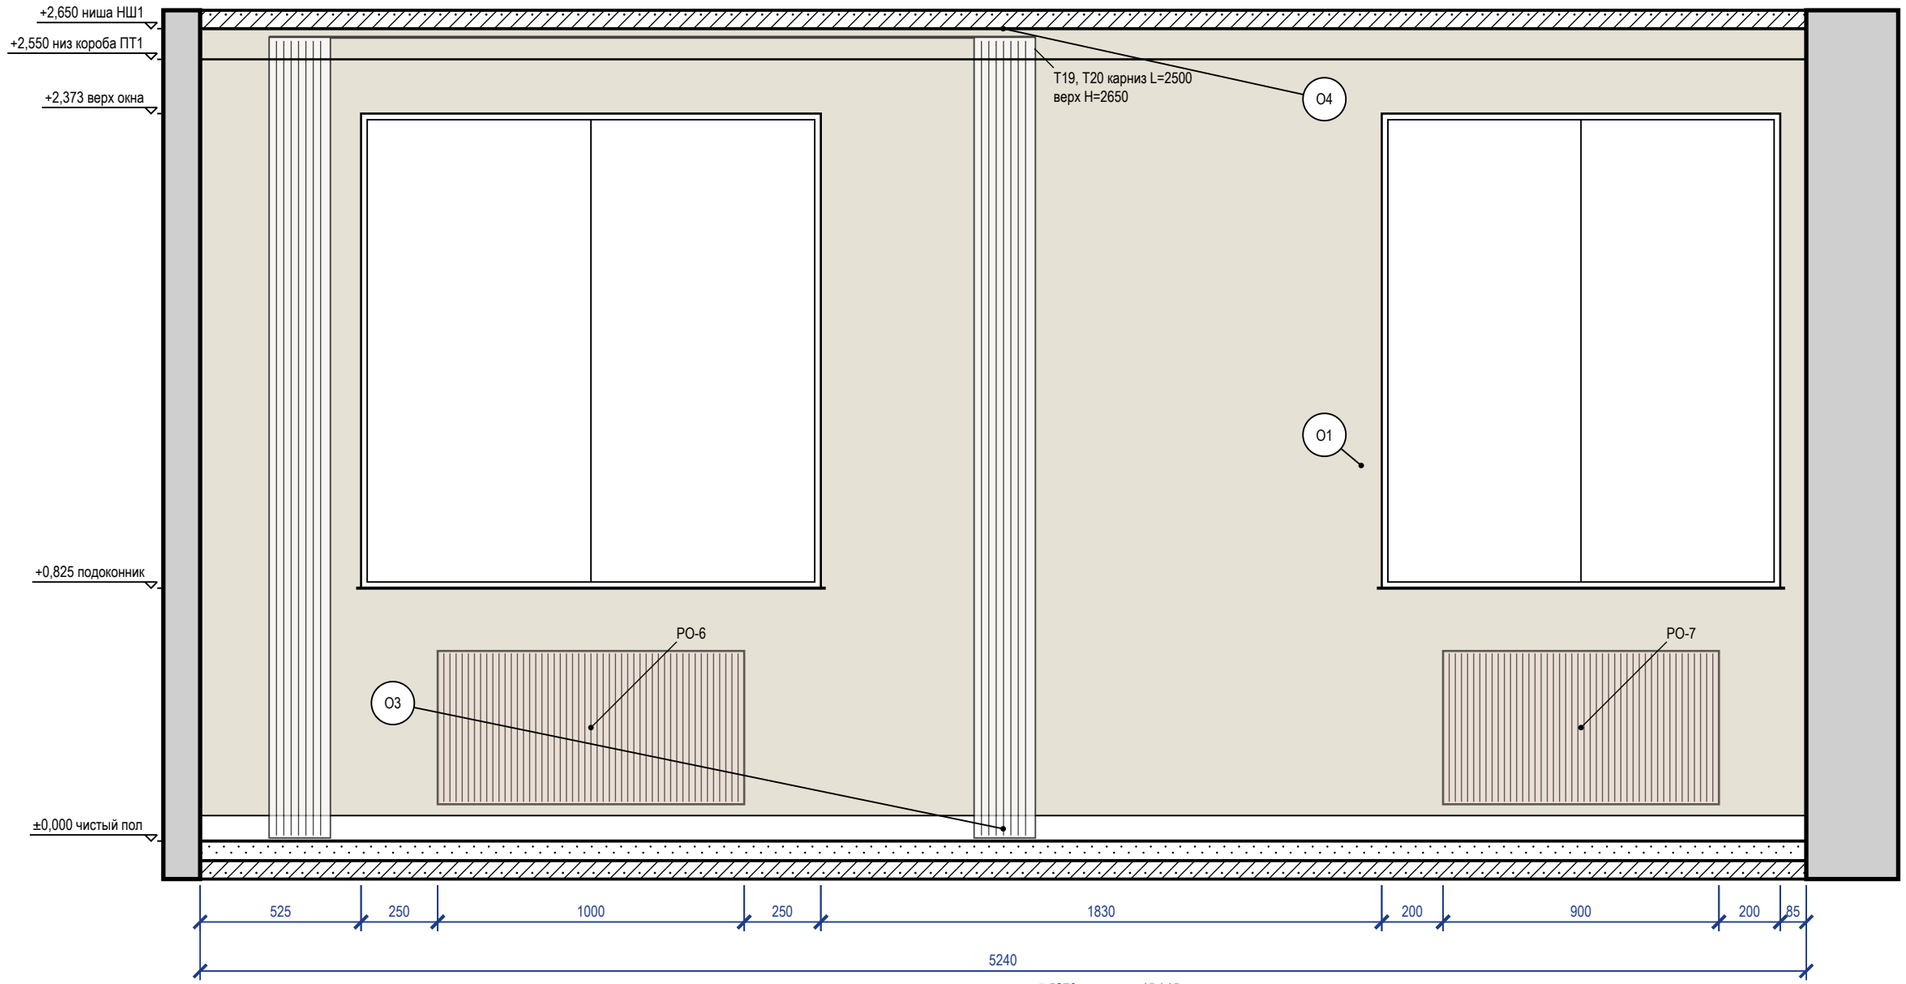


Схема развёрток (М 1:100)

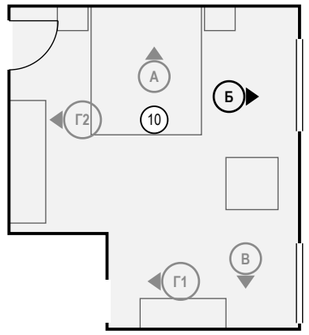

Ведомость отделки (на листе)

Марка	Поверхность	Материал, изделие	Цвет, код	Кол.
О1	стены	окраска, Farrow & Ball Modern Emulsion, матовая, подготовка Q3	Farrow & Ball No. 291 «School House White тёплый меловой белый»	9,6 м²
О3	плинтус	плинтус МДФ, h 83 мм, Ultrawood Base 5340, ЛДФ под окраску, 83×15 мм, 2440 мм (арт. LDF-BASE-5340)	Farrow & Ball No. 291 «School House White тёплый меловой белый»	5,2 м
О4	потолок	окраска, Tikkurila Anti-Reflex 2, глубокоматовая, подготовка Q3	NCS S 0502-Y «Белый с лёгкой желтизной»	22,5 м²

Примечания

1. Размеры — в мм от чистовых поверхностей стен; условные обозначения и общие указания — лист 3.
2. Карнизы (шины) — по ведомости текстиля декоратора: длина L и верх H на развёртке — те же числа, что в ведомости; крепление — до окраски потолка.

					Проект: Квартира 103 м²	М 1:20
	Лист	№ док.	Подпись	Дата	Развёртка стены Б. Спальня мастер (пом. 10)	Стадия / Лист / Листов
Дизайнер	Кырлан А.С.			04.11.26		П / 76 / 96

Развёртка стены В


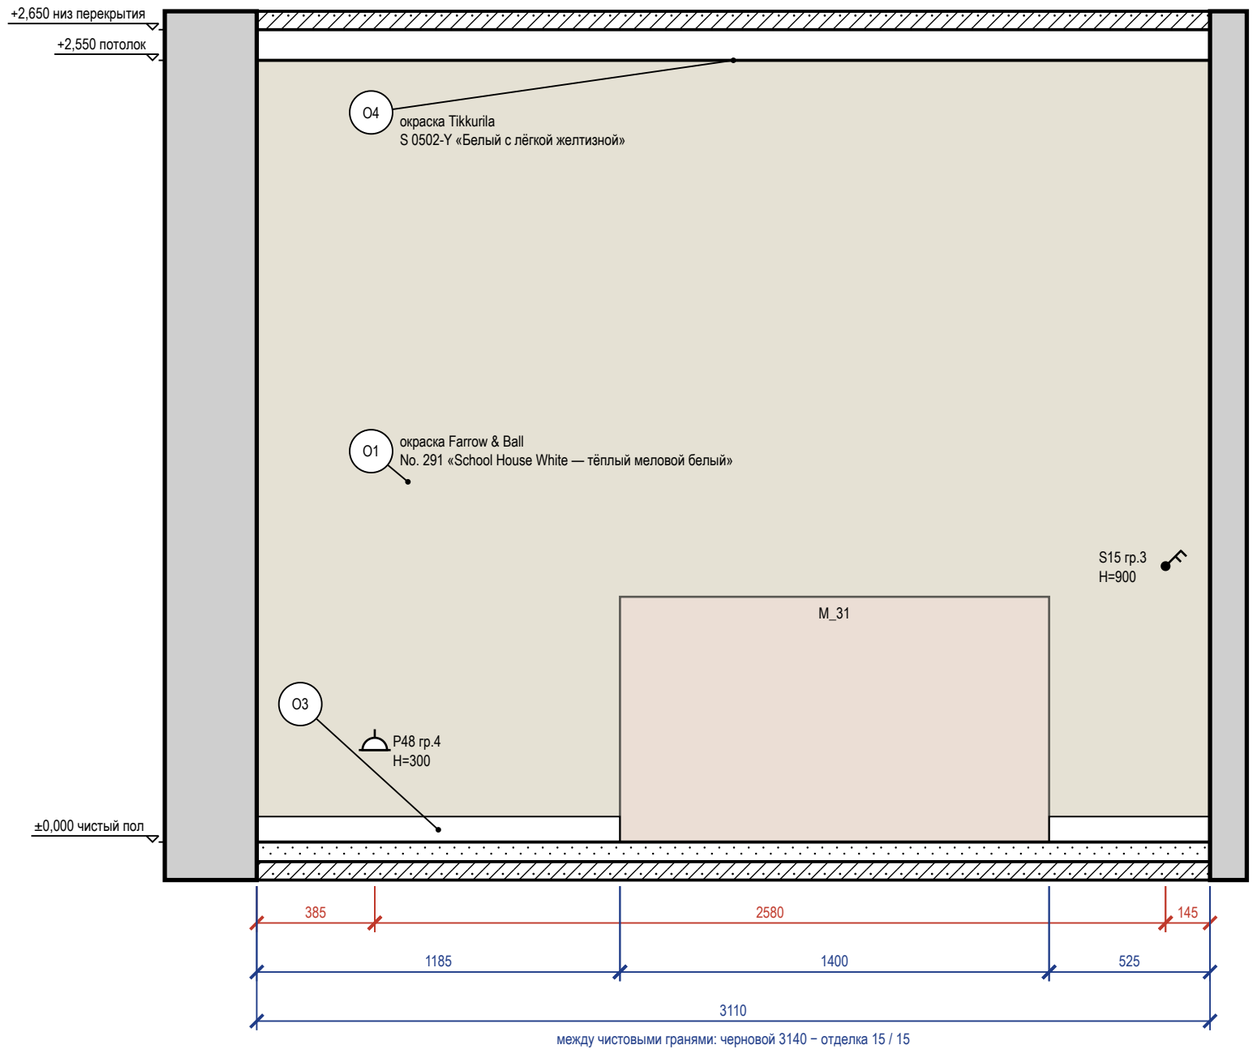


Схема развёрток (М 1:100)

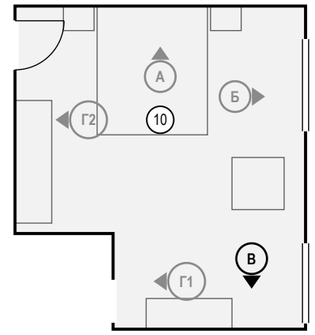

Ведомость отделки (на листе)

Марка	Поверхность	Материал, изделие	Цвет, код	Кол.
О1	стены	окраска, Farrow & Ball Modern Emulsion, матовая, подготовка Q3	Farrow & Ball No. 291 «School House White — тёплый меловой белый»	7,9 м²
О3	плинтус	плинтус МДФ, h 83 мм, Ultrawood Base 5340, ЛДФ под окраску, 83×15 мм, 2440 мм (арт. LDF-BASE-5340)	Farrow & Ball No. 291 «School House White — тёплый меловой белый»	1,7 м
О4	потолок	окраска, Tikkurila Anti-Reflex 2, глубокоматовая, подготовка Q3	NCS S 0502-Y «Белый с лёгкой желтизной»	22,5 м²

Примечания

1. Размеры — в мм от чистовых поверхностей стен; условные обозначения и общие указания — лист 3.

	Лист	№ док.	Подпись	Дата
Дизайнер	Кырлан А.С.			04.11.26

Проект: Квартира 103 м² — **М 1:20**

Развёртка стены В. Спальня мастер (пом. 10)

Стадия	Лист	Листов
П	77	96

выпуск 04.11.2026 № d6a6e5e88d · стр. 77 из 96

Развёртка стены Г1


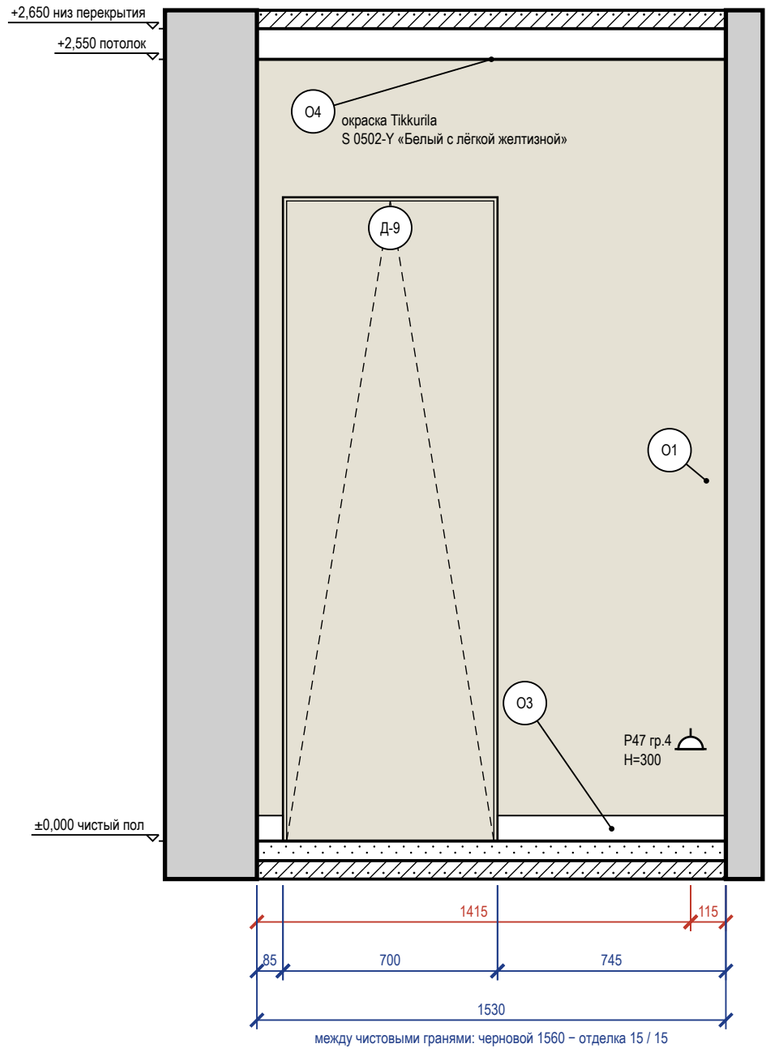


Схема развёрток (М 1:100)

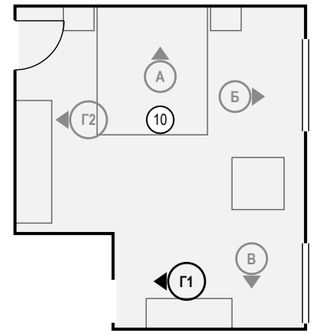

Ведомость отделки (на листе)

Марка	Поверхность	Материал, изделие	Цвет, код	Кол.
О1	стены	окраска, Farrow & Ball Modern Emulsion, матовая, подготовка Q3	Farrow & Ball No. 291 «School House White — тёплый меловой белый»	2,4 м²
О3	плинтус	плинтус МДФ, h 83 мм, Ultrawood Base 5340, ЛДФ под окраску, 83×15 мм, 2440 мм (арт. LDF-BASE-5340)	Farrow & Ball No. 291 «School House White — тёплый меловой белый»	0,8 м
О4	потолок	окраска, Tikkurila Anti-Reflex 2, глубокоматовая, подготовка Q3	NCS S 0502-Y «Белый с лёгкой желтизной»	22,5 м²

Примечания

1. Размеры — в мм от чистовых поверхностей стен; условные обозначения и общие указания — лист 3.
2. Двери скрытого монтажа — полотно в плоскости стены, отделка стены по полотну, плинтус прерывается у короба (узел — на листе узлов).

	Лист	№ док.	Подпись	Дата
Дизайнер	Кырлан А.С.			04.11.26

Проект: Квартира 103 м² — **М 1:20**

Развёртка стены Г1. Спальня мастер (пом. 10)

Стадия	Лист	Листов
П	78	96

Развёртка стены Г2


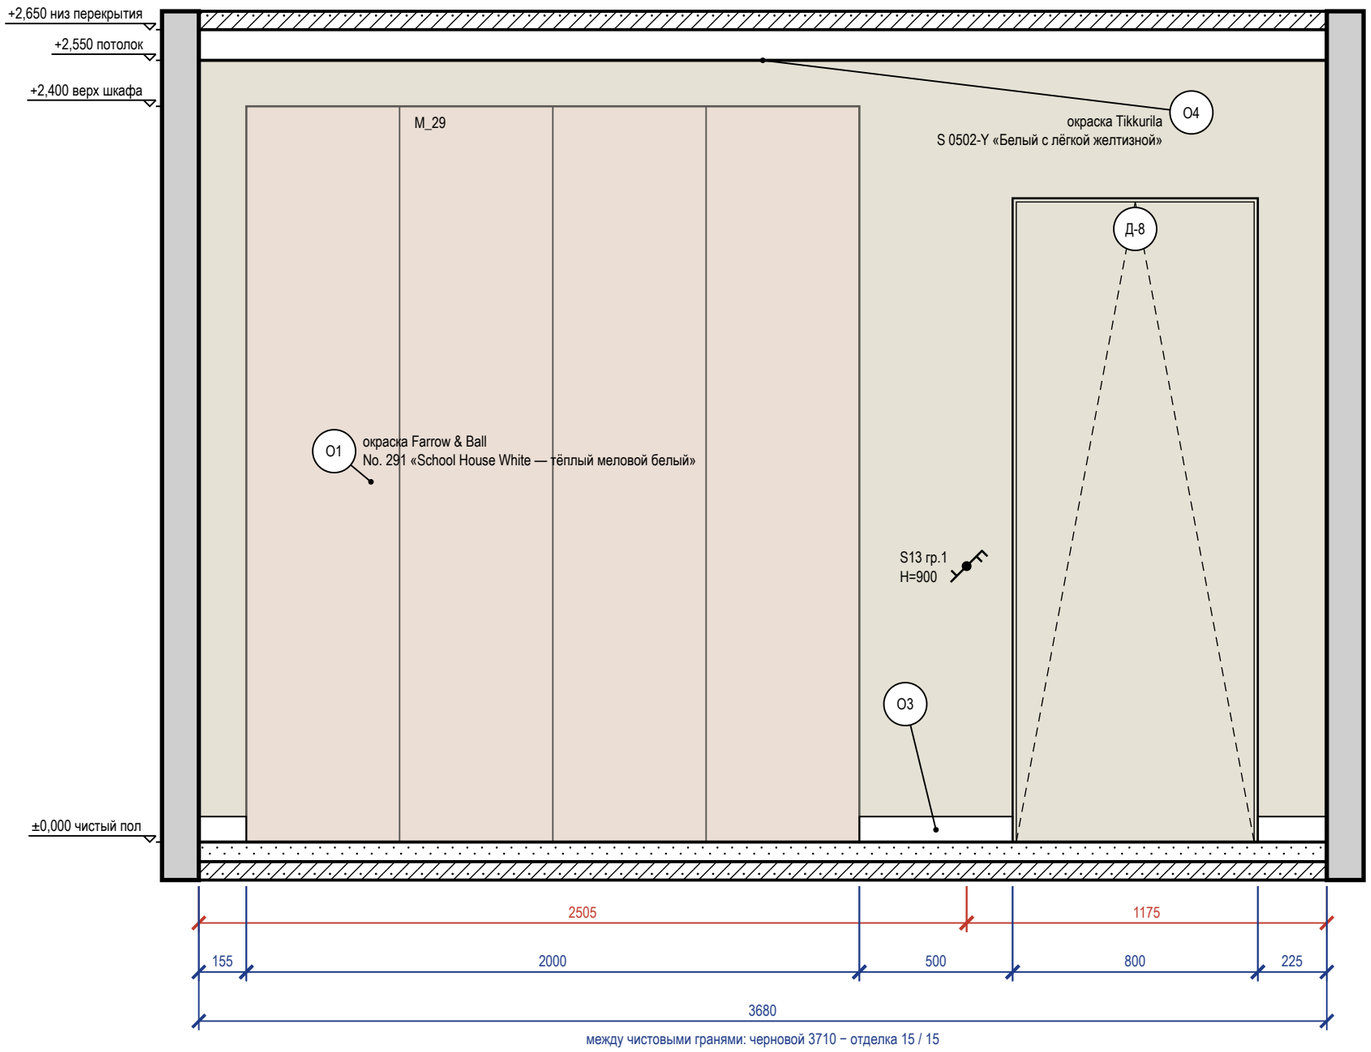


Схема развёрток (М 1:100)

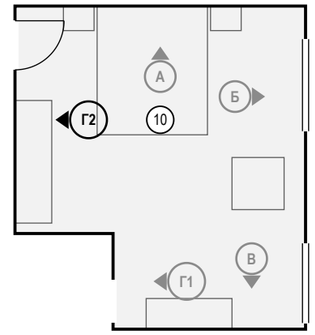

Ведомость отделки (на листе)

Марка	Поверхность	Материал, изделие	Цвет, код	Кол.
О1	стены	окраска, Farrow & Ball Modern Emulsion, матовая, подготовка Q3	Farrow & Ball No. 291 «School House White — тёплый меловой белый»	7,7 м²
О3	плинтус	плинтус МДФ, h 83 мм, Ultrawood Base 5340, ЛДФ под окраску, 83×15 мм, 2440 мм (арт. LDF-BASE-5340)	Farrow & Ball No. 291 «School House White — тёплый меловой белый»	0,9 м
О4	потолок	окраска, Tikkurila Anti-Reflex 2, глубокоматовая, подготовка Q3	NCS S 0502-Y «Белый с лёгкой желтизной»	22,5 м²

Примечания

1. Размеры — в мм от чистовых поверхностей стен; условные обозначения и общие указания — лист 3.
2. Двери скрытого монтажа — полотно в плоскости стены, отделка стены по полотну, плинтус прерывается у короба (узел — на листе узлов).


	Лист	№ док.	Подпись	Дата
Дизайнер	Кырлан А.С.			04.11.26

Проект: Квартира 103 м² — **М 1:20**


Развёртка стены Г2. Спальня мастер (пом. 10)

Стадия	Лист	Листов
П	79	96

Развёртка стены А

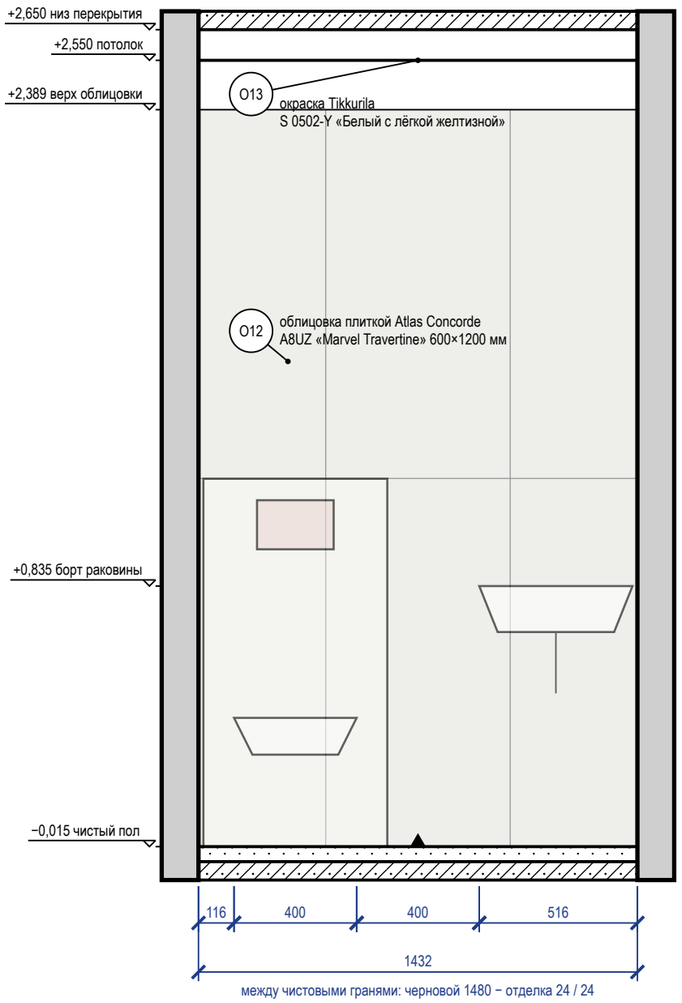

Развёртка стены Б

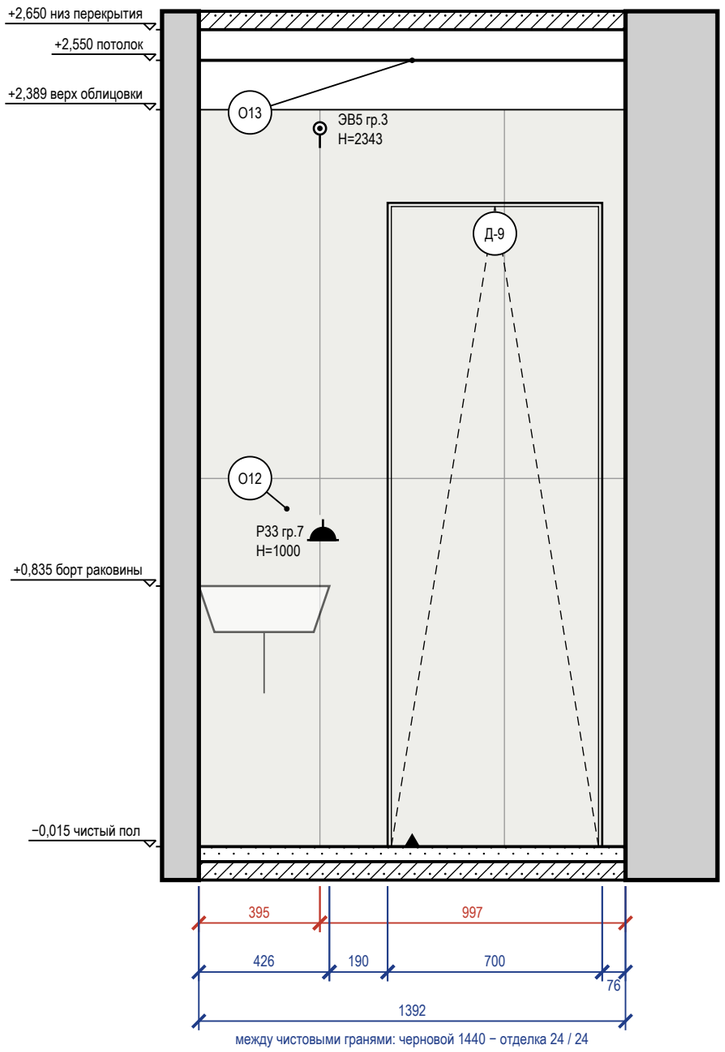

Развёртка стены В


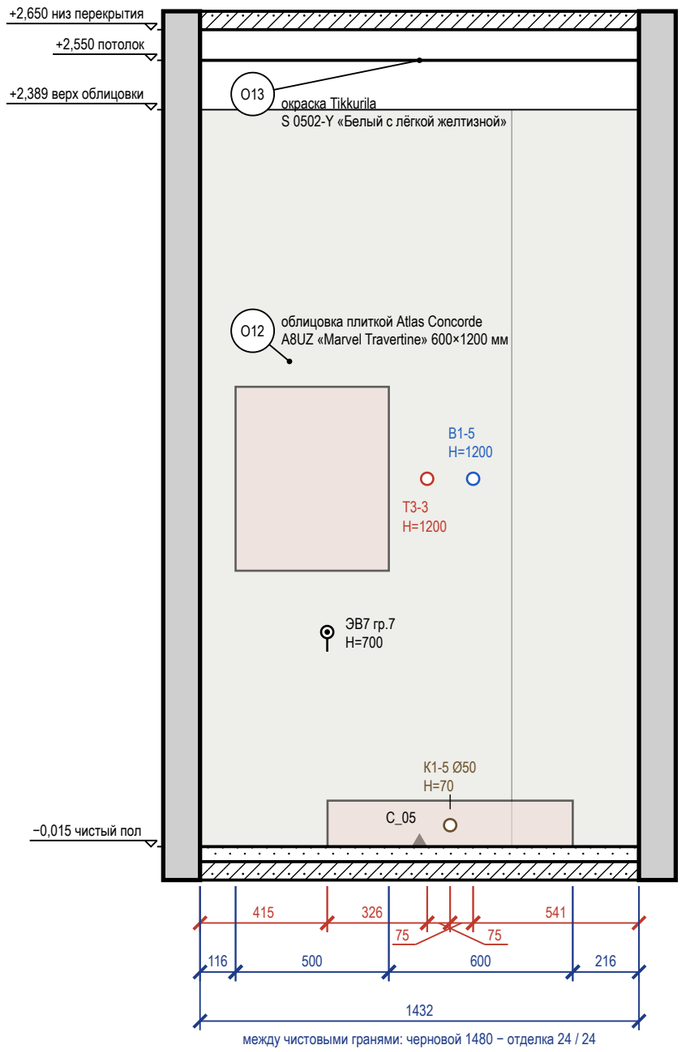


Схема развёрток (М 1:100)

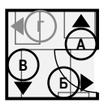

Ведомость отделки (на листе)

Марка	Поверхность	Материал, изделие	Цвет, код	Кол.
О12	стены	облицовка плиткой, Atlas Concorde Marvel Travertine, 600×1200×9 мм, A8UZ, затирка CG2WA	Atlas Concorde A8UZ «Marvel Travertine»	8,8 м²
О13	потолок	окраска, Tikkurila Luja 7, матовая, подготовка Q3	NCS S 0502-Y «Белый с лёгкой желтизной»	2,1 м²

Примечания

1. Размеры — в мм от чистовых поверхностей стен; условные обозначения и общие указания — лист 3.
2. Стена А показана двумя видами: здесь — архитектурная развёртка (мебель, отделка, проёмы, высоты), электроточки и выводы ВК с привязками и таблицей — на листе 81 («Привязки»).
3. Схема мебели, приборов и декора не является технической документацией для производства мебели; габариты — по паспортам изделий.
4. Выводы ВК — коды и высоты по листу выводов сантехники.
5. Облицовка — по сетке швов 2 мм, раскладка от оси стены (треугольник у пола), целые ряды от пола; подрезки — по листу раскладки плитки.
6. Гидроизоляция в 2 слоя, заход на стены 200 мм; у душа — до 2000 и 500 мм за поддон — до облицовки, с актом скрытых работ и тестом проливом (узел — на листе узлов).
7. Двери скрытого монтажа — полотно в плоскости стены, отделка стены по полотну, плинтус прерывается у короба (узел — на листе узлов).
8. Линии узора (швы плитки, складки штор, рёбра радиаторов) прерываются у знаков и выносок — просвет между линиями не менее 0,7 мм.

					Проект: Квартира 103 м²	М 1:20
	Лист	№ док.	Подпись	Дата		
Дизайнер	Кырлан А.С.			04.11.26	Развёртки стен А, Б, В. Ванная мастер (пом. 11)	Стадия: П; Лист: 80; Листов: 96

Развёртка стены А: электроточки и выводы

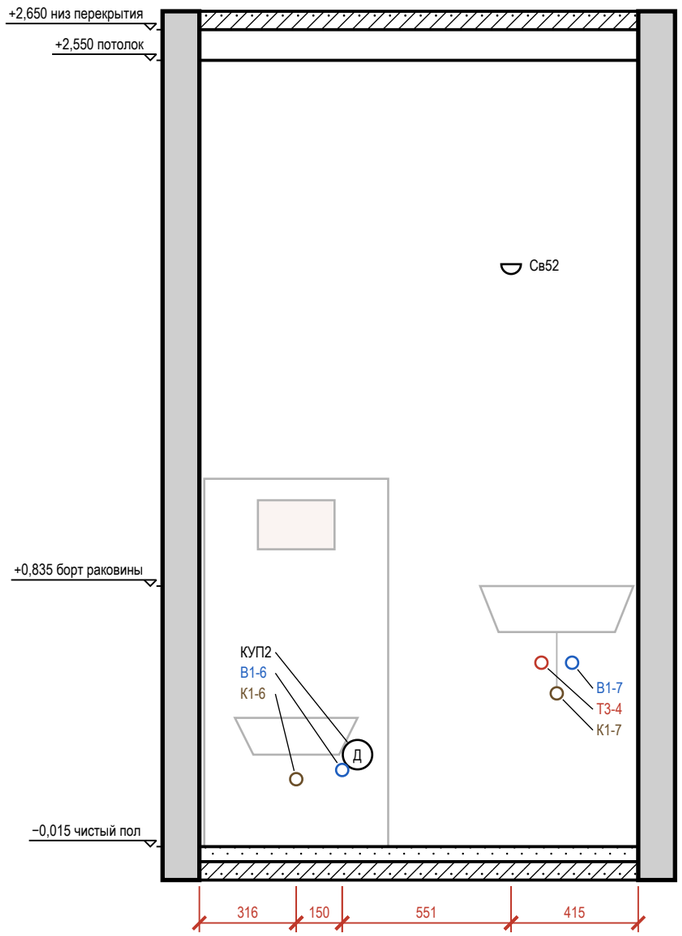



Таблица привязок электроточек и выводов

Марка	Назначение	От угла, мм	H от пола, мм	Примечание
К1-6	канализация — унитаз подвесной	316	220	Ø110
В1-6	холодная вода — унитаз подвесной	466	250	в раме инсталляции
КУП2	КУП — уравнивание потенциалов (ДСУП)	516	300	
Св52	светильник настенный	1017	1900	гр. 3
Т3-4	горячая вода — умывальник	1116	600	межос. 100
К1-7	канализация — умывальник	1166	500	Ø50
В1-7	холодная вода — умывальник	1216	600	межос. 100

Условные обозначения

- светильник настенный (бра), H — высота оси
- вывод В1 (код — в ведомости привязок)
- вывод Т3 (код — в ведомости привязок)
- вывод К1 (код — в ведомости привязок)
- привязки точек и выводов от угла и от пола, мм
- марка развёртки: буква стены, стрелка — взгляд

Схема развёрток (М 1:50)

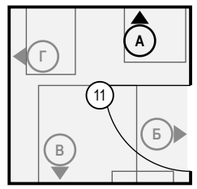

Примечания

1. Вид «Привязки» стены А — электроточки и выводы ВК; архитектурная развёртка (мебель, отделка, проёмы, высоты) — на листе 80. Мебель и приборы — подложкой для ориентира; их марки и обозначения мебели, проёмов и стен — там же.
2. Привязки — в мм: по горизонтали от левого чистового угла стены до оси изделия, H — от чистого пола до оси; все точки — в таблице привязок. Красная цепочка — привязки по осям; точки ближе 120 мм одна к другой в цепочку не дробятся — их привязки только в таблице.
3. У знака — марка электроточки (Р — розетка, S — выключатель, Св — светильник, ЭВ — вывод кабеля); условные обозначения и общие указания — лист 3.
4. Коды выводов ВК: В1 — холодная вода, Т3 — горячая вода, К1 — канализация; номер после дефиса — номер вывода на листе выводов сантехники.

					Проект: Квартира 103 м²	М 1:20
	Лист	№ док.	Подпись	Дата	Привязки электроточек и выводов ВК, стена А. Ванная мастер (пом. 11)	Стадия / Лист / Листов
Дизайнер	Кырлан А.С.			04.11.26		П / 81 / 96

Развёртка стены Г

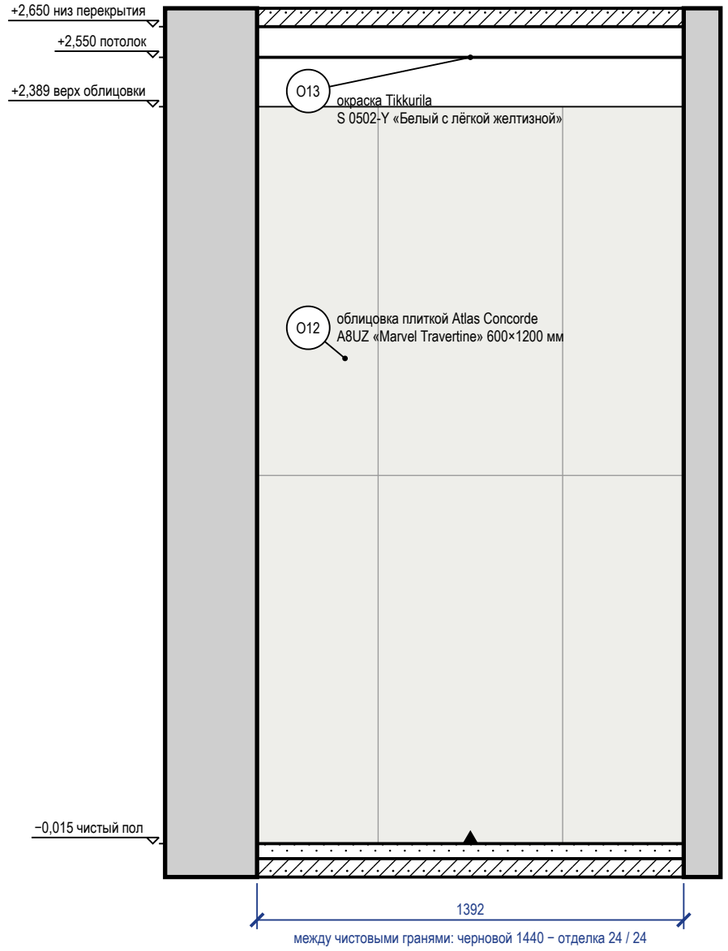


Схема развёрток (М 1:100)



Ведомость отделки (на листе)

Марка	Поверхность	Материал, изделие	Цвет, код	Кол.
O12	стены	облицовка плиткой, Atlas Concorde Marvel Travertine, 600×1200×9 мм, A8UZ, затирка CG2WA	Atlas Concorde A8UZ «Marvel Travertine»	3,3 м²
O13	потолок	окраска, Tikkurila Luja 7, матовая, подготовка Q3	NCS S 0502-Y «Белый с лёгкой желтизной»	2,1 м²

Примечания

1. Размеры — в мм от чистовых поверхностей стен; условные обозначения и общие указания — лист 3.
2. Облицовка — по сетке швов 2 мм, раскладка от оси стены (треугольник у пола), целые ряды от пола; подрезки — по листу раскладки плитки.
3. Гидроизоляция в 2 слоя, заход на стены 200 мм; у душа — до 2000 и 500 мм за поддон — до облицовки, с актом скрытых работ и тестом проливом (узел — на листе узлов).

					Проект: Квартира 103 м²	М 1:20
	Лист	№ док.	Подпись	Дата	Развёртка стены Г. Ванная мастер (пом. 11)	Стадия / Лист / Листов
Дизайнер	Кырлан А.С.			04.11.26		П / 82 / 96

Комплект предварительный по пунктам этих таблиц. Пока по пункту нет ответа или решения, показанное на указанном листе — допущение проектировщика, а не утверждённое решение.
Сводка: открытых вопросов — 7 (из них ждут факта объекта — 4: контрольного обмера, обследования или документа); изменений в реестре — 1, из них без подписи — 1.

Открытые вопросы и принятые допущения

№	Формулировка	Вид	Кто решает	Если решения нет	Лист, где это проявляется
К-1	Размеры сняты со скана обмерного плана KV оформление (в см): часть подписей не читается, помещения выровнены по читаемым размерам. До заказа мебели, дверей и материалов нужен контрольный обмер.	Отсутствует Ждёт: обмера	Архитектор-планировщик	размеры на листах — по плану заказчика, уточняются по месту; мебель на заказ и материалы по ним не заказывать	л. 5 — План планировки от заказчика л. 13 — План размещения мебели и оборудования
К-2	Высота потолка принята 2650 мм по отметкам обмера (Н = 2,50…2,66 м); под ригелем 2,28 м — уточнить.	Отсутствует	Архитектор-планировщик	высоты на развёртках и потолки — от 2650 мм, уточнить при обмере	л. 5 — План планировки от заказчика л. 32 — План потолков
К-4	Разрешённая мощность объединённой квартиры по ТУ неизвестна, принята 15 кВт; при объединении двух квартир ТУ переоформляются.	Отсутствует	Инженер-электрик	щит и группы рассчитаны на 15 кВт; при меньших ТУ пересчёт	л. 36 — Однолинейная схема щита л. 37 — План розеток и электровыводов
К-5	Объединение двух квартир в одну (проём в межквартирной стене между гостиной и коридором правой квартиры, вход — один из тамбура, второй вход закрывается; правая кухня — постирочная) — предложение проектировщика. Межквартирная стена, колонны и ригель — несущие или нет, неизвестно (на обмере отмечены «несущие колонны» и «ригель перекрытия»): нужны поэтажный план БТИ, техзаключение и согласование перепланировки (ЖК РФ ст. 25–29).	Отсутствует Ждёт: документа	Архитектор-планировщик	проём и перегородки — предложение, к строительству не выдаются; мокрые зоны и кухня оставлены на местах обмера	л. 5 — План планировки от заказчика
К-6	Ванная мастер (пом. 11): стояки Ст К1-3 Ø110, Ст В1-3, Ст Т3-3 по данным стоят в углу стен В и Г (оси ≈ 90–240 мм от стены Г, 150–280 мм от стены В) — внутри габарита душевого поддона С_05 800 × 800 у стены В, а душ со стеклоблочной перегородкой по плану сохраняется. Поддон на стояки не встанет, короба (зазор 50 мм) и люка 300 × 400 к арматуре нет. Положение стояков снято со скана обмера (К-1), отдельно не замерялось. Нужен контрольный обмер угла: оси стояков от двух стен, перегородка из стеклоблоков. Затем решить: (а) короб стояков в углу ≈ 310 × 350 с люком, поддон 800 × 800 сдвинуть вдоль стены В от короба, стеклоблочную перегородку разобрать и выложить заново по новому поддону; (б) поддон меньше, вне короба (по месту после обмера); (в) душ с трапом без поддона по обходу короба.	Спорно Ждёт: обмера, затем решения	Инженер ВК (вода, канализация)	душевую зону С_05, поддон и перегородку не выполнять; выводы С_05 и короб стояков — после обмера	л. 18 — План выводов сантехники л. 19 — Схема разводки водопровода и канализации л. 5 — План планировки от заказчика
К-7	Унитаз подвесной С_02 (пом. 6 «Ванная»), выпуск К1-2 Ø110: трасса до Ст К1-1 (1,91 м) идёт под дверным проёмом Д-5 — короб над полом там не поставить. Решить: (а) прибор ближе к стояку Ст К1-1 (без прохода под проёмом); (б) выпуск в полу с подъёмом пола помещения на 160 мм; (в) насосная установка (КНС) у прибора — по паспорту, требует согласования. Решение меняет санузел (высоты, раскладку плитки) — за автором с заказчиком.	Спорно Ждёт: решения	Инженер ВК (вода, канализация)	выпуск К1-2 и прибор С_02 не выполнять до решения; остальное — по листам	л. 19 — Схема разводки водопровода и канализации л. 18 — План выводов сантехники
К-8	Климатический подрайон (СП 131.13330) не задан: принят не северный — жилые комнаты и кухня под потолком от 2,5 м (СП 54, п. 5.12); в IA, IБ, IГ, IД, IVA — от 2,7 м.	Отсутствует Ждёт: документа	Архитектор-планировщик	отметки потолков жилых — по 2,5 м; при северном подрайоне уровни ниже 2,7 м пересчитать до заказа каркаса	л. 32 — План потолков

Изменения проекта после выпуска листов (реестр изменений)

№	Дата	Лист	Было	Стало	Кто решил, подпись
ИЗ-1	30.10.2026	л. 36 — Однолинейная схема щита л. 37 — План розеток и электровыводов л. 28 — Раскладка плитки. Ванная. Развёртки стен л. 30 — План размещения дверей л. С3 — Спецификация отделочных материалов л. 18 — План выводов сантехники	Фены Р8, Р33 и полотенцесушители В6, В7 сидели на гр. 13 «посудомоечная машина», стиральная машина Р50 — на гр. 12 «духовой шкаф»; групп 7 и 8 в щите не было. Два вывода печатались «ЭВ4» (духовой шкаф «ЭВ4» на кухне и вентилятор «В4» ванной). Окно 2 спальни мастер (смещение 3500, 1300) выходило за стену Б (3830). Пол ванных и плинтус МДФ — без артикула. Стояки Ст К1-3/В1-3/Т3-3 без признака допущения.	Группы 7 (санузлы: фены, полотенцесушители, УЗО 10 мА) и 8 (стиральная машина постирочной) добавлены, точки переназначены. Выводы кухни — В1 (варочная), В2 (духовой шкаф), печать ЭВ1/ЭВ2 — марки на листах уникальны. Окно 2 — стена Б части 1, смещение 100, знак «*» (К-1). Пол ванных — Marvel Travertine Sand Cross 60×60 AFUL, плинтус — Ultrawood Base 5340 83×15. Стояки ванной мастер — assumed, К-6; остаётся до обмера.	Не утверждено: подписи нет. решение исполнителя; на утверждение А. С. Кырлана


Примечания

1. Номера листов — по ведомости рабочих чертежей комплекта (лист «Общие данные»).
2. Графа «Если решения нет» показывает состояние решения на листах; влияние на сроки и стоимость по пунктам не оценивалось.
3. Пункт, по которому принято решение, при следующем выпуске комплекта из таблиц исключается.


					Проект: Квартира 103 м²
	Лист	№ док.	Подпись	Дата	Открытые вопросы, принятые допущения и конфликты
Дизайнер	Кырлан А.С.			04.11.26	

Стадия	Лист	Листов
П	83	96


Общий вид

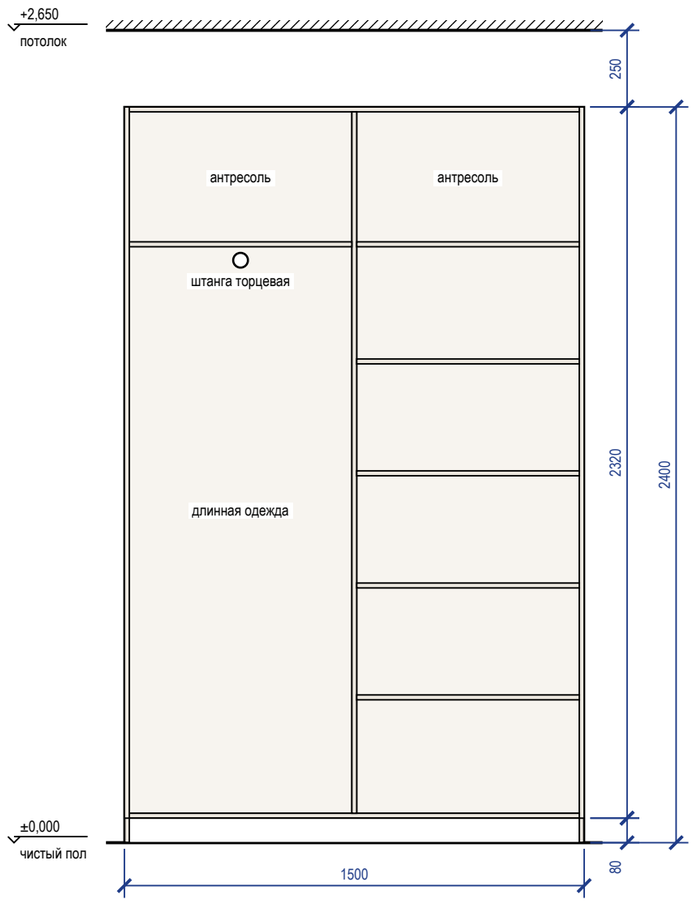


Наполнение, размеры в свету

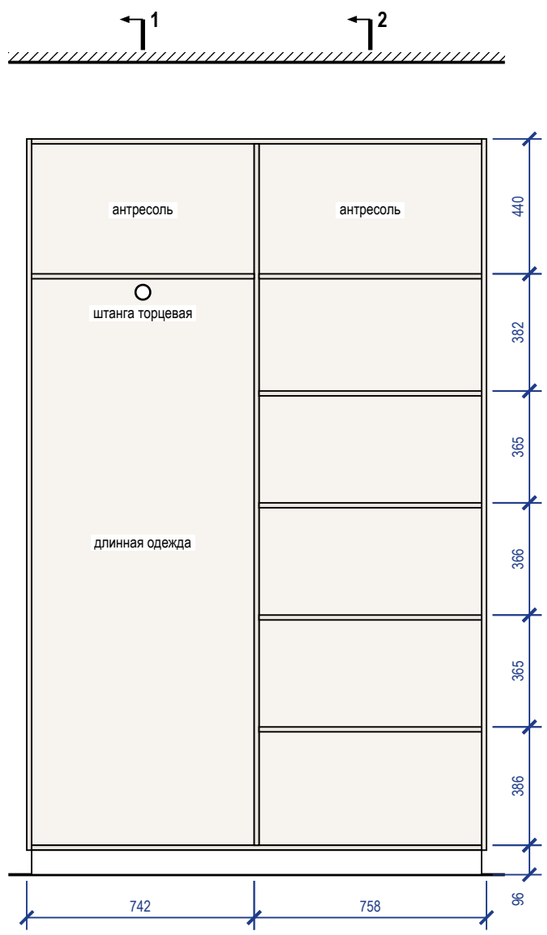

Разрез 1-1

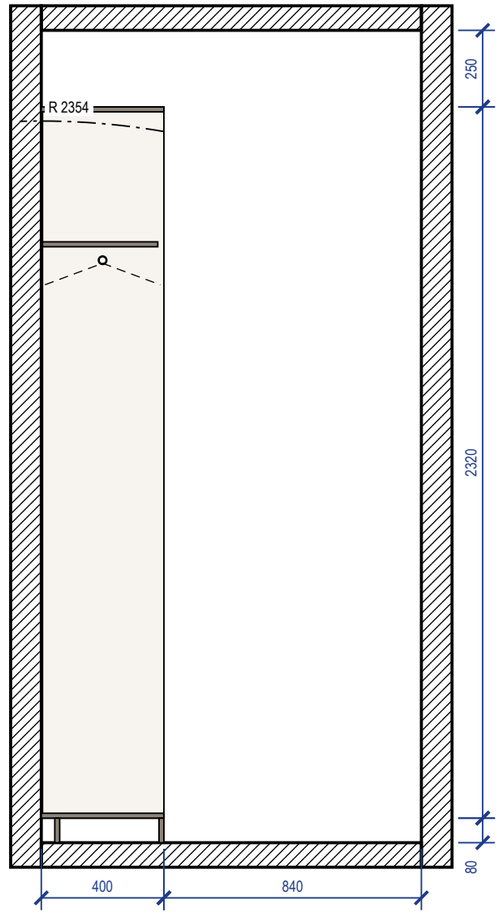


Разрез 2-2

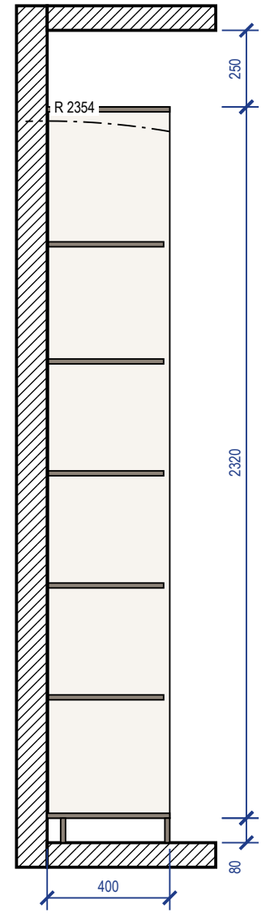

Примечания


1. Размеры — в мм по чистовой отделке; изделие 1500×400×2400 (Ш×Г×В). Перед раскроем — контрольный замер цеха после чистовой отделки стен, пола и потолка.
2. Корпус — ЛДСП декор «орех» 16 мм, задняя стенка ХДФ 4 мм в паз, цоколь 80 мм на регулируемых опорах; открытая система: без фасадов.
3. Кромка: скрытые торцы 0,4 мм, видимые 2 мм (ПВХ/АБС).
4. Присадка по 32-й системе — выполняет цех.
5. Зазор до потолка 250 мм.
6. Подъём корпуса: диагональ боковины без цоколя $\sqrt{(2320^2 + 400^2)} = 2354$ мм < 2650 мм до потолка — корпус собирается лёжа, поднимается поворотом и ставится на цоколь.
7. Крепление к стене от опрокидывания — уголки 2 шт. к несущему основанию (монтажная схема шкафов).
8. Проход перед изделием 840 мм показан на разрезе 1-1.

3D орто

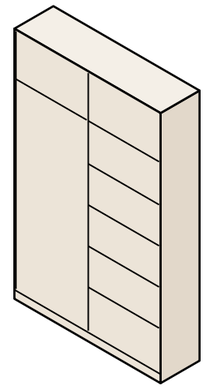


					Проект: Квартира 103 м²	**М 1:20**
	Лист	№ док.	Подпись	Дата	Система хранения М_05	Стадия / Лист / Листов
Дизайнер	Кырлан А.С.			04.11.26		П / Д_1 / 96


Вид с фасадами

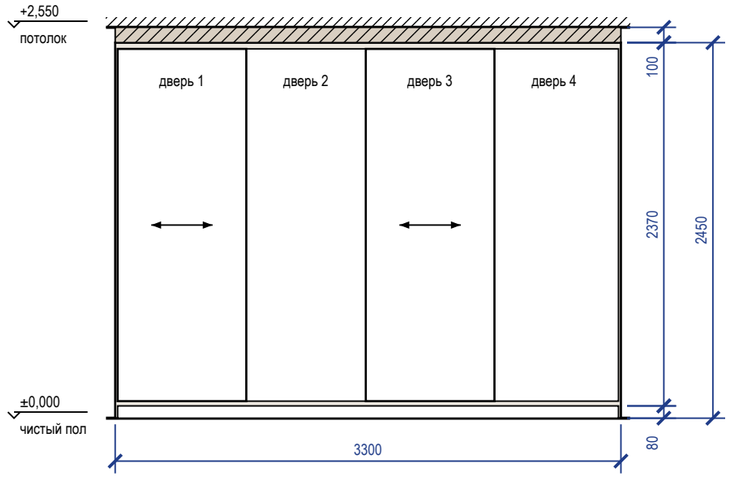


Вид без фасадов

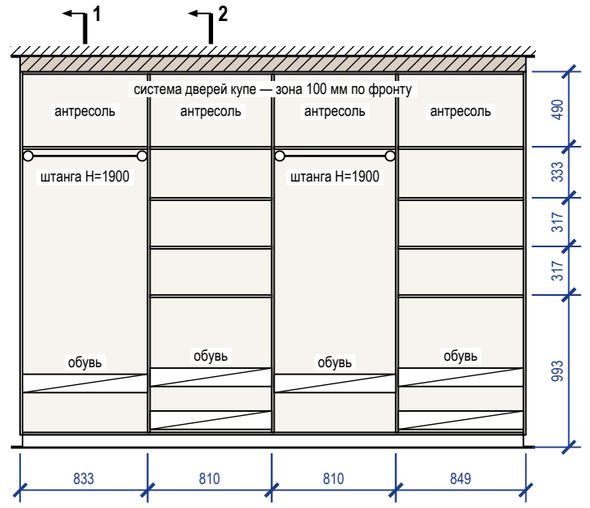

Разрез 1-1

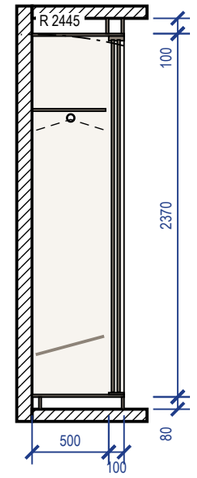


Разрез 2-2

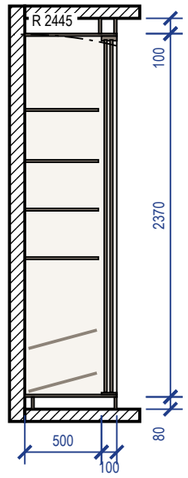

Примечания


1. Размеры — в мм по чистовой отделке; изделие 3300×600×2450 (Ш×Г×В). Перед раскроем — контрольный замер цеха после чистовой отделки стен, пола и потолка.
2. Корпус — ЛДСП 16 мм, задняя стенка ХДФ 4 мм в паз, цоколь 80 мм на регулируемых опорах; двери купе — МДФ, шпон ореха 10 мм, масло матовое в профиле: латунь; нахлёст 30 мм, ширина двери 840 мм, высота — проём минус 40 мм; цвет — по колерной карте.
3. Кромка: скрытые торцы 0,4 мм, видимые 2 мм (ПВХ/АБС).
4. Номинальные зазоры: дверь купе — боковина 3 мм, фасад ящика — стойка 2 мм; ящики внутри купе — с накладкой 30 мм на стойке со стороны нахлёста дверей.
5. Присадка по 32-й системе — выполняет цех.
6. Компенсатор 100 мм — короб из ЛДСП по фронту и торцам, подгоняется к потолку при монтаже (припуск 20 мм), крепится к корпусу и к потолку.
7. Подъём корпуса: диагональ боковины без цоколя $\sqrt{(2370^2 + 600^2)} = 2445$ мм < 2550 мм до потолка — корпус собирается лёжа, поднимается поворотом и ставится на цоколь.
8. Крепление к стене от опрокидывания — уголки 2 шт. к несущему основанию (монтажная схема шкафов).

3D орто

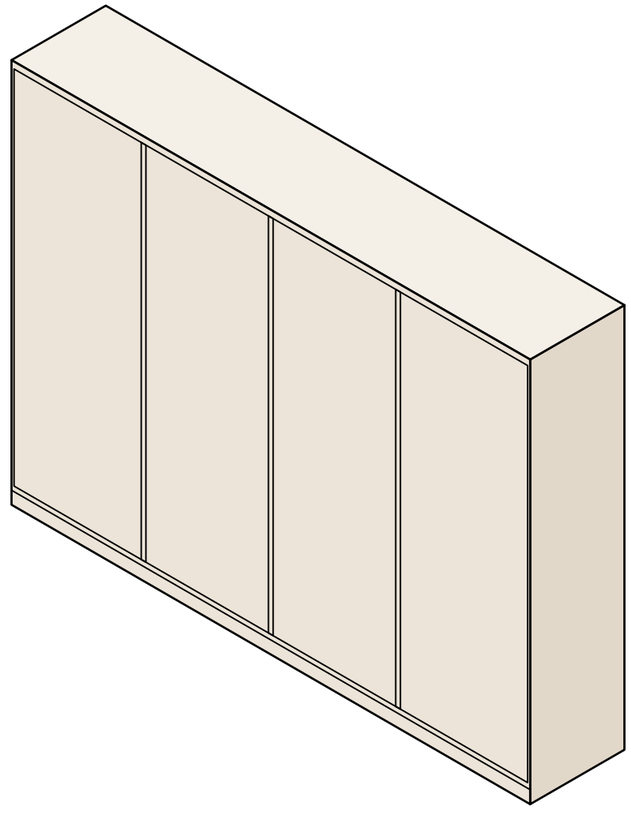


					Проект: Квартира 103 м²	**М 1:40**
	Лист	№ док.	Подпись	Дата		
Дизайнер	Кырлан А.С.			04.11.26	Шкаф-купе М_11	Стадия: П; Лист: Д_2; Листов: 96


Общий вид

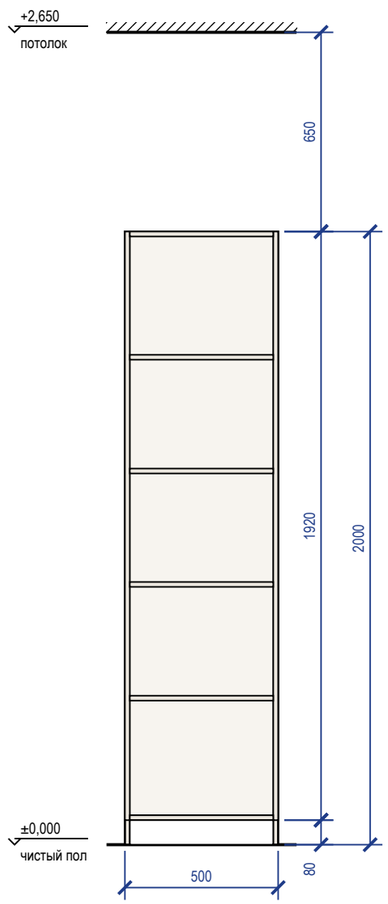

Наполнение, размеры в свету

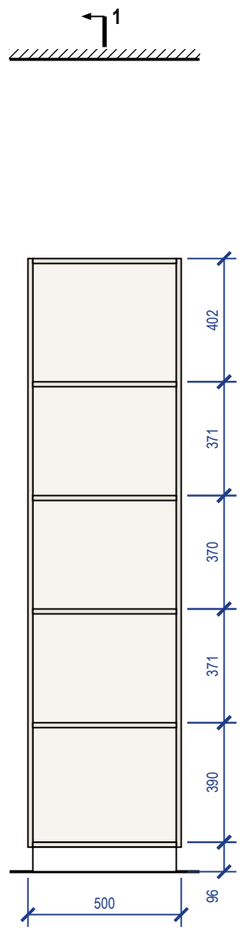


Разрез 1-1

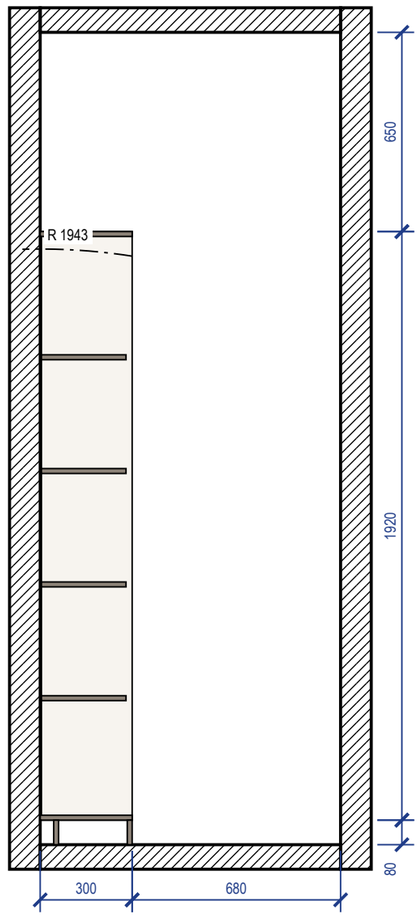

Примечания


1. Размеры — в мм по чистовой отделке; изделие 500×300×2000 (Ш×Г×В). Перед раскроем — контрольный замер цеха после чистовой отделки стен, пола и потолка.
2. Корпус — ЛДСП 16 мм, задняя стенка ХДФ 4 мм в паз, цоколь 80 мм на регулируемых опорах; открытая система: без фасадов.
3. Кромка: скрытые торцы 0,4 мм, видимые 2 мм (ПВХ/АБС).
4. Присадка по 32-й системе — выполняет цех.
5. Зазор до потолка 650 мм.
6. Подъём корпуса: диагональ боковины без цоколя $\sqrt{(1920^2 + 300^2)} = 1943$ мм < 2650 мм до потолка — корпус собирается лёжа, поднимается поворотом и ставится на цоколь.
7. Крепление к стене от опрокидывания — уголки 2 шт. к несущему основанию (монтажная схема шкафов).
8. Проход перед изделием 680 мм показан на разрезе 1-1.

3D орто

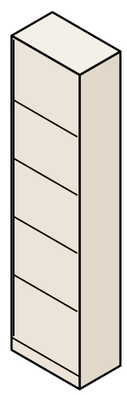


					Проект: Квартира 103 м²	**М 1:20**
	Лист	№ док.	Подпись	Дата	Система хранения М_22	
Дизайнер	Кырлан А.С.			04.11.26	Стадия: П	Лист: Д_3 / Листов: 96


Вид с фасадами

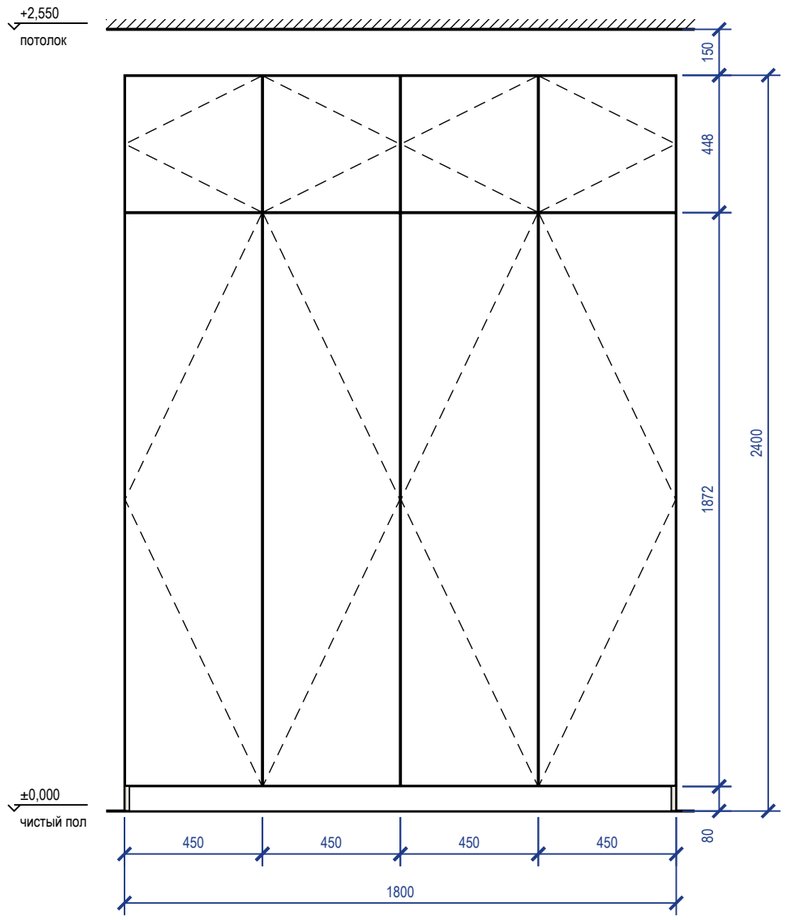


Вид без фасадов

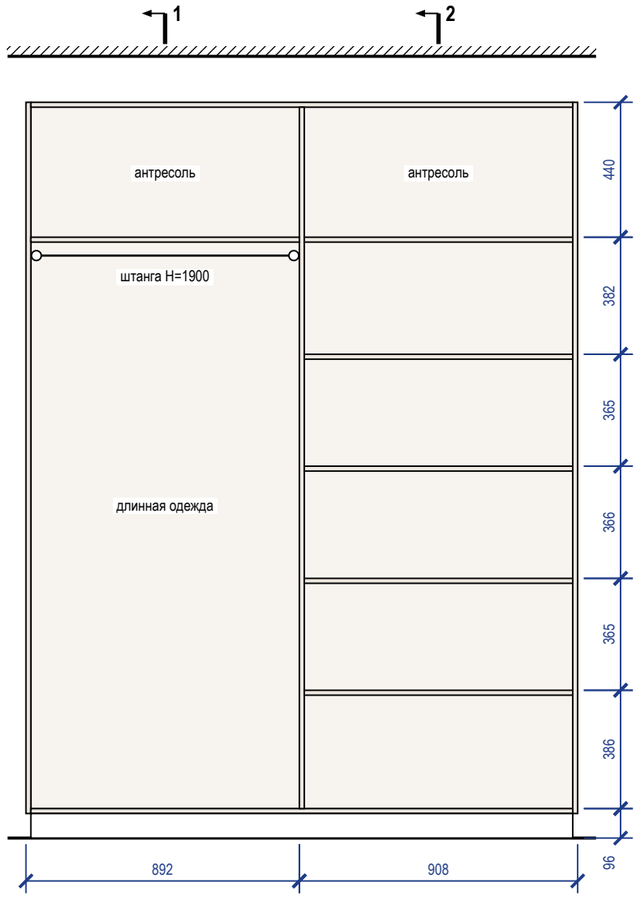

Разрез 1-1

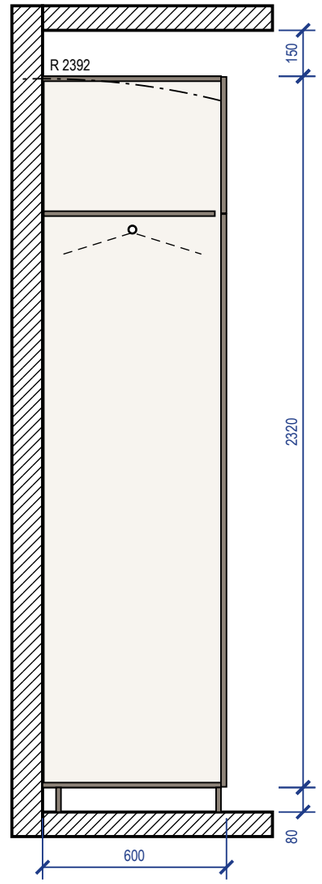


Разрез 2-2

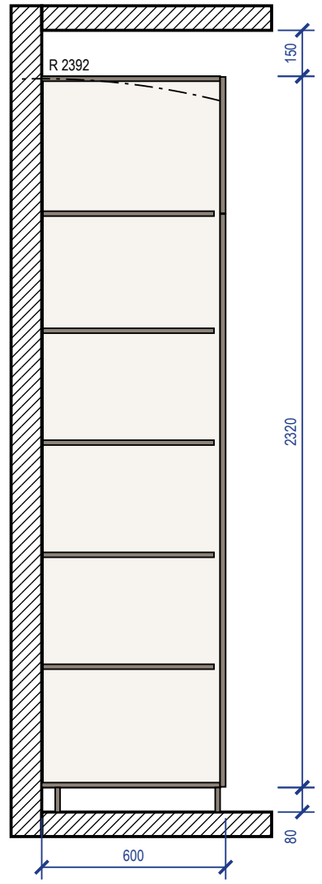

Примечания


1. Размеры — в мм по чистовой отделке; изделие 1800×600×2400 (Ш×Г×В). Перед раскроем — контрольный замер цеха после чистовой отделки стен, пола и потолка.
2. Корпус — ЛДСП 16 мм, задняя стенка ХДФ 4 мм в паз, цоколь 80 мм на регулируемых опорах; фасады накладные — МДФ, шпон ореха 18 мм, масло матовое; цвет — по колерной карте; петли с доводчиком: фасад 1869 мм — 4 петли, фасад 445 мм — 2 петли.
3. Кромка: скрытые торцы 0,4 мм, видимые 2 мм (ПВХ/АБС).
4. Номинальные зазоры: между фасадами 3 мм, фасад — стена и фасад — потолок не менее 3 мм, фасад ящика — стойка 2 мм.
5. Присадка по 32-й системе — выполняет цех.
6. Зазор до потолка 150 мм — закрыть планкой в цвет корпуса при монтаже.
7. Подъём корпуса: диагональ боковины без цоколя $\sqrt{(2320^2 + 582^2)} = 2392$ мм < 2550 мм до потолка — корпус собирается лёжа, поднимается поворотом и ставится на цоколь.
8. Крепление к стене от опрокидывания — уголки 2 шт. к несущему основанию (монтажная схема шкафов).

3D орто

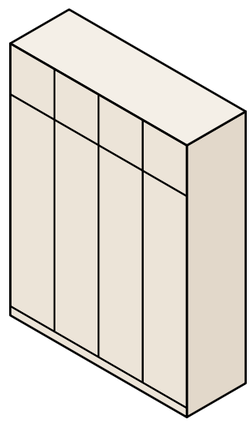


					Проект: Квартира 103 м²	М 1:20
	Лист	№ док.	Подпись	Дата		
Дизайнер	Кырлан А.С.			04.11.26	Шкаф распашной М_24	Стадия: П; Лист: Д_4; Листов: 96


Вид с фасадами

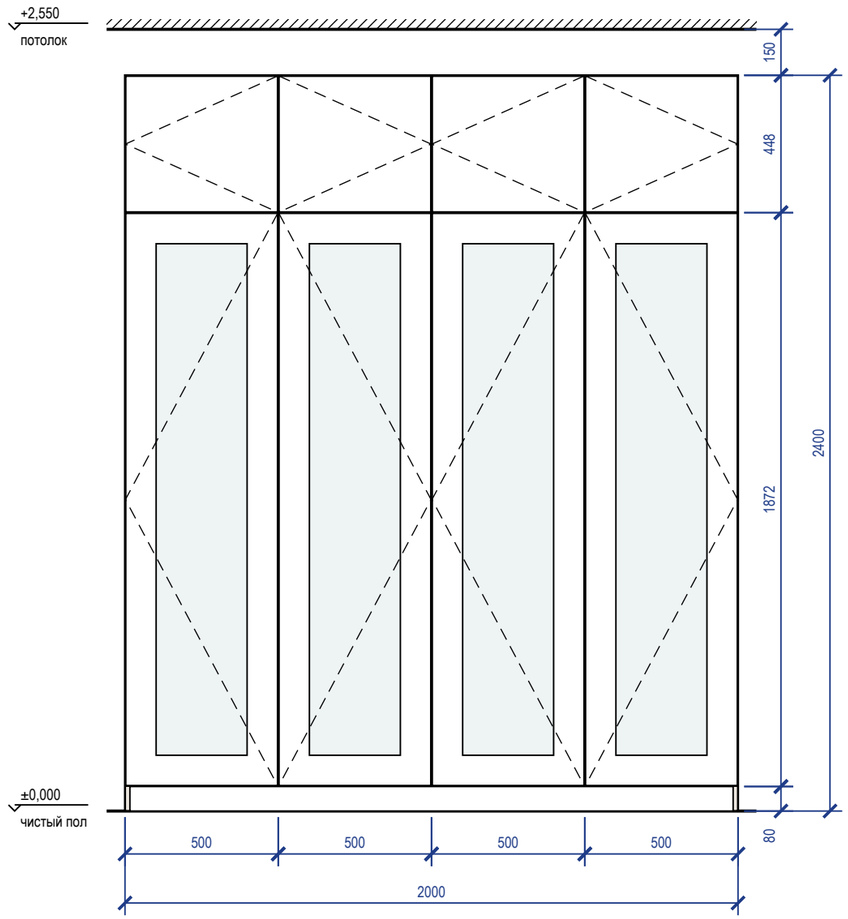


Вид без фасадов

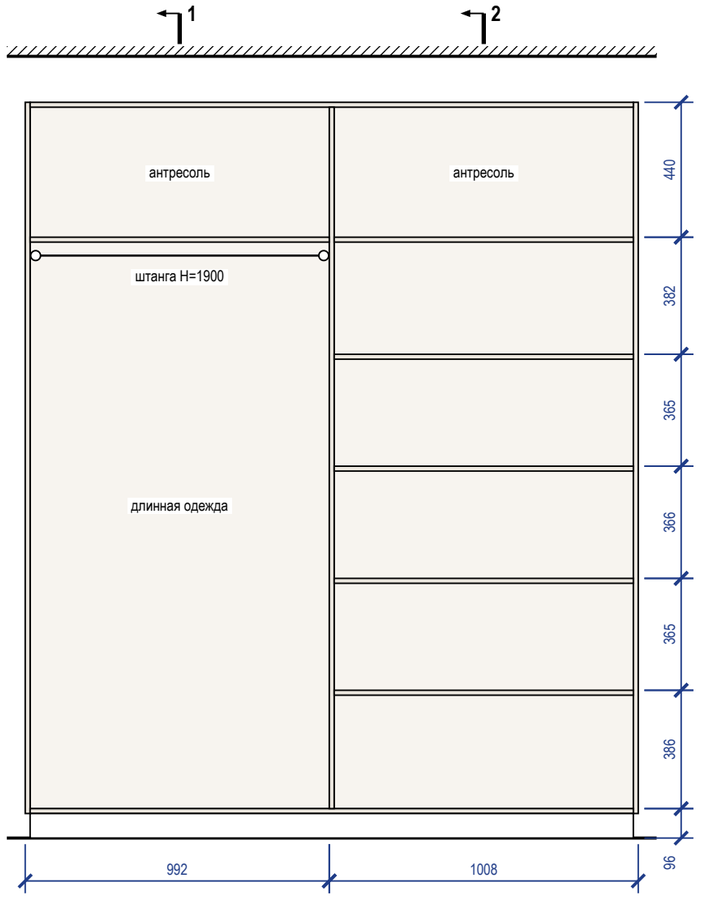

Разрез 1-1

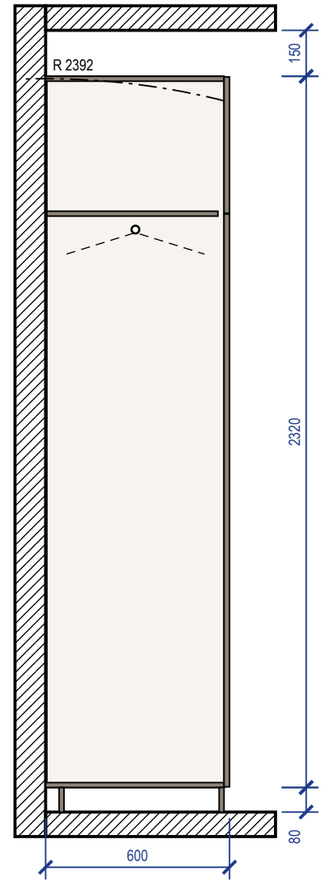


Разрез 2-2

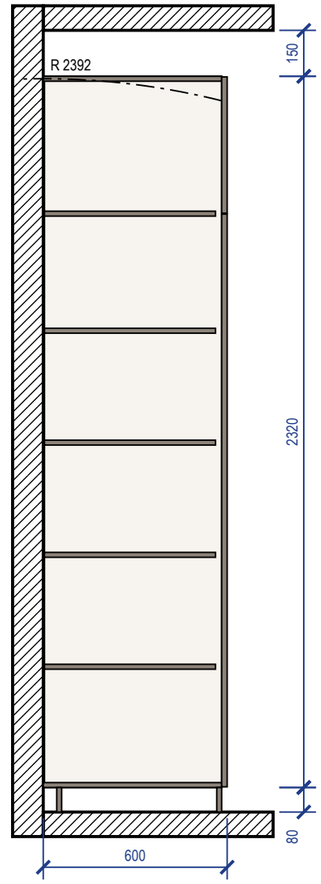

Примечания

1. Размеры — в мм по чистовой отделке; изделие 2000×600×2400 (Ш×Г×В). Перед раскроем — контрольный замер цеха после чистовой отделки стен, пола и потолка.
2. Корпус — ЛДСП 16 мм, задняя стенка ХДФ 4 мм в паз, цоколь 80 мм на регулируемых опорах; фасады накладные — МДФ, шпон ореха 18 мм, масло матовое; вставка — латунь; цвет — по колерной карте; петли с доводчиком: фасад 1869 мм — 4 петли, фасад 445 мм — 2 петли.
3. Кромка: скрытые торцы 0,4 мм, видимые 2 мм (ПВХ/АБС).
4. Номинальные зазоры: между фасадами 3 мм, фасад — стена и фасад — потолок не менее 3 мм, фасад ящика — стойка 2 мм.
5. Присадка по 32-й системе — выполняет цех.
6. Зазор до потолка 150 мм — закрыть планкой в цвет корпуса при монтаже.
7. Подъём корпуса: диагональ боковины без цоколя $\sqrt{(2320^2 + 582^2)} = 2392$ мм < 2550 мм до потолка — корпус собирается лёжа, поднимается поворотом и ставится на цоколь.
8. Крепление к стене от опрокидывания — уголки 2 шт. к несущему основанию (монтажная схема шкафов).


3D орто

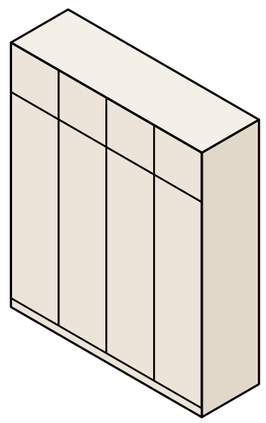


					Проект: Квартира 103 м²	**М 1:20**
	Лист	№ док.	Подпись	Дата	Шкаф распашной М_29	Стадия / Лист / Листов
Дизайнер	Кырлан А.С.			04.11.26		П / Д_5 / 96

выпуск 04.11.2026 № d6a6e5e88d · стр. 88 из 96


Вид с фасадами

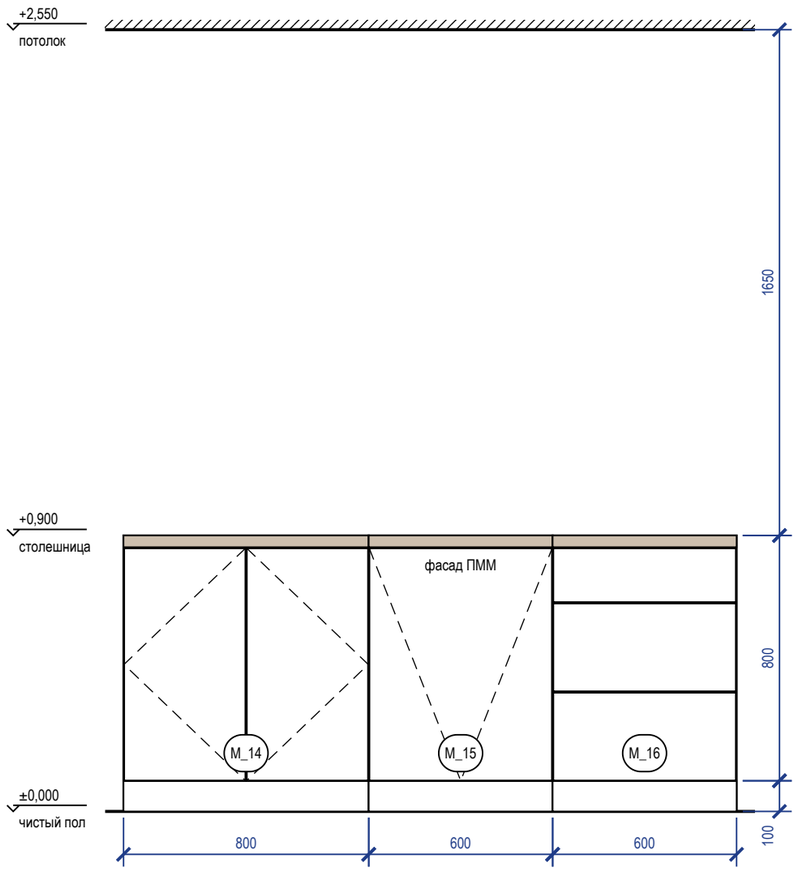


Вид без фасадов (наполнение, выводы)

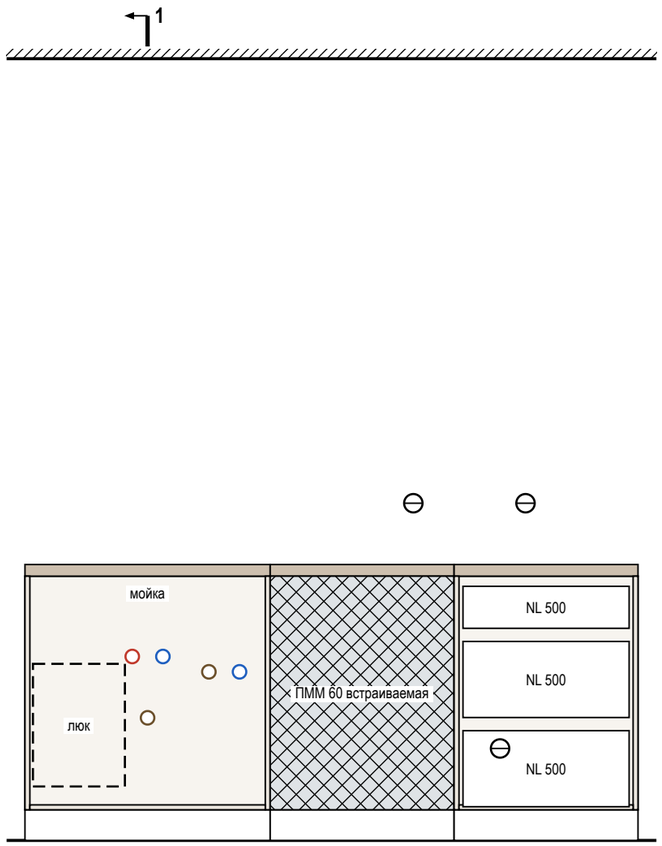

Разрез 1-1

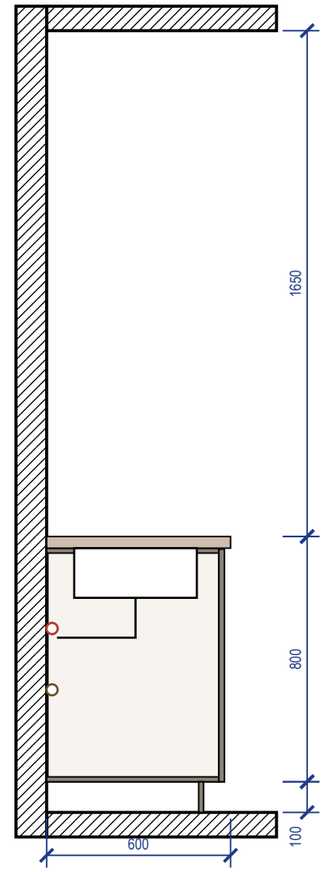

3D орто

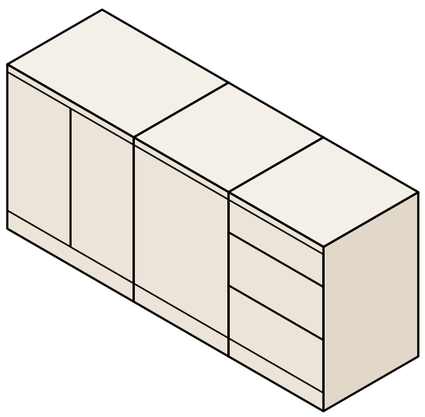


Примечания

1. Размеры — в мм по чистовой отделке, вид из помещения; марки — как на плане расстановки. Перед раскроем — контрольный замер цеха после фартука и пола.
2. Корпуса — ЛДСП 16 мм, задняя стенка ХДФ 4 мм; фасады — МДФ, шпон ореха 18 мм, цвет по колерной карте; столешница 38 мм, свес 20 мм; цоколь 100 мм.
3. Кромка: скрытые торцы 0,4 мм, видимые 2 мм. Номинальные зазоры: между фасадами 3 мм, фасад — столешница 3 мм, фасад — стена не менее 3 мм.
4. Ящики полного выдвижения и петли — с доводчиком; присадка по 32-й системе — выполняет цех.
5. Ниши техники — по монтажным схемам выбранных моделей: решётка в цоколе и канал за пеналом холодильника, зазор за духовым шкафом, фасад ПММ на двери машины.
6. M_14: сервисный люк к стоякам Ст К1-2 (кухня), Ст В1-2, Ст Т3-2 — съёмная панель 300×400 мм в задней стенке на саморезах (по виду без фасадов, штриховой контур «люк»), доступ через фасад модуля; короб стояков за модулем — с ревизией напротив люка (лист ВК).


					Проект: Квартира 103 м²	М 1:20
	Лист	№ док.	Подпись	Дата	Кухня (пом. 5). Развёртка гарнитура	
Дизайнер	Кырлан А.С.			04.11.26		

Стадия	Лист	Листов
П	Д_6	96


Вид с фасадами

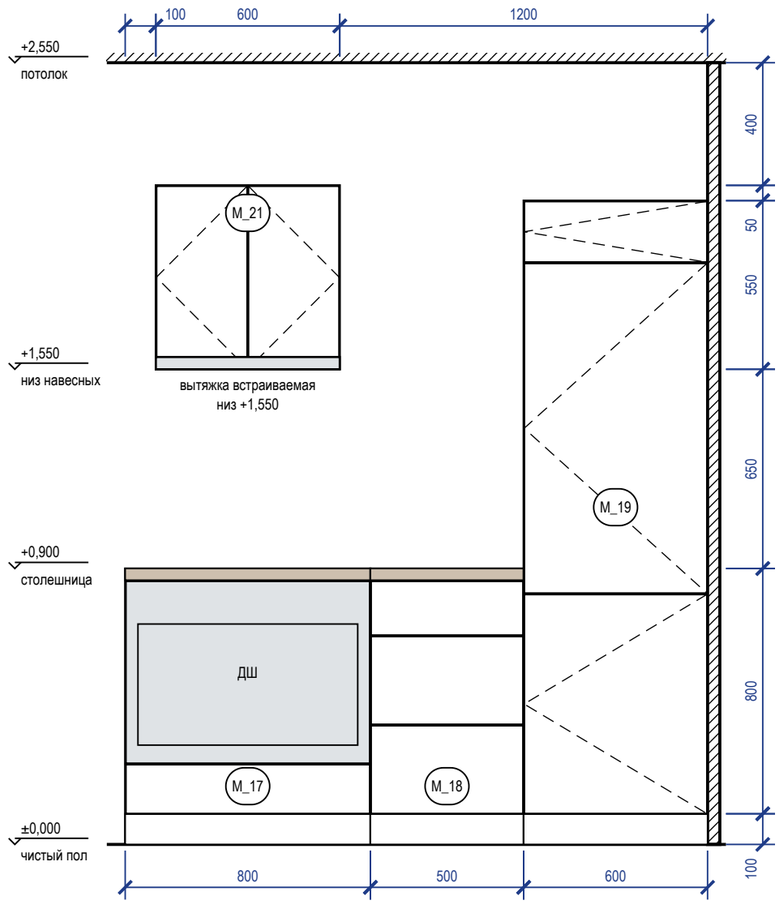


Вид без фасадов (наполнение, выводы)

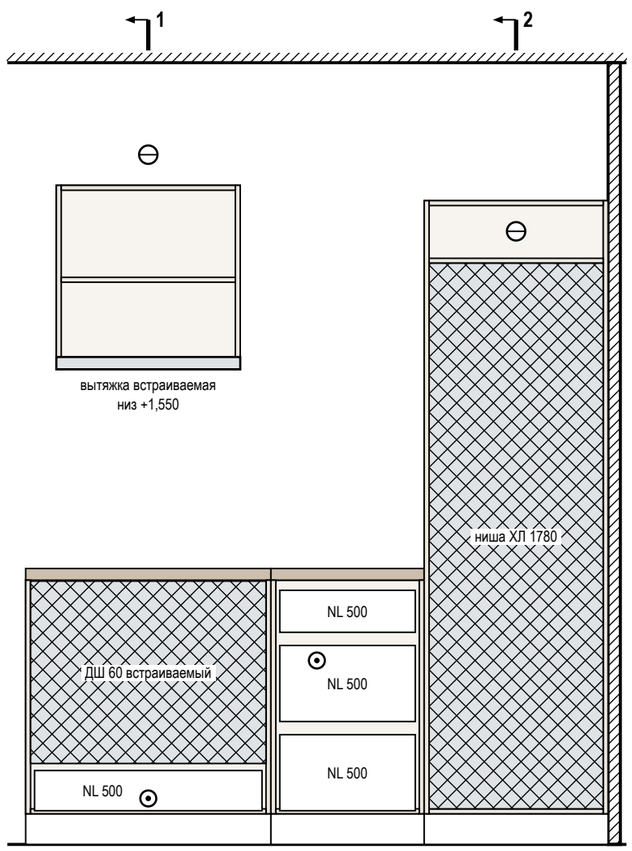


Разрез 1-1

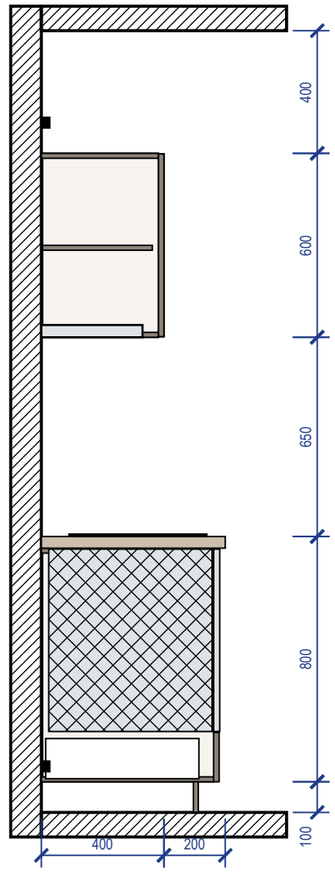

Разрез 2-2

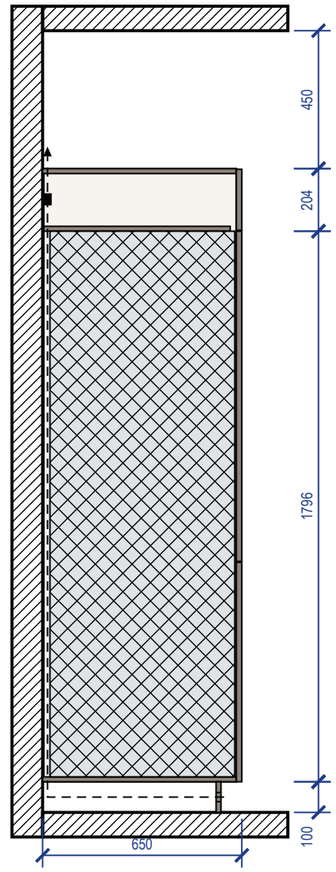

3D орто

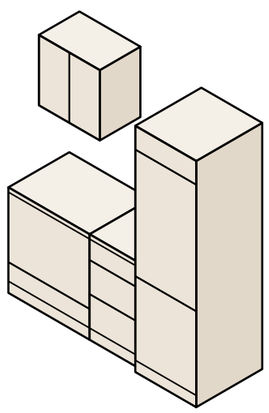

Примечания

1. Размеры — в мм по чистовой отделке, вид из помещения; марки — как на плане расстановки. Перед раскроем — контрольный замер цеха после фартука и пола.
2. Корпуса — ЛДСП 16 мм, задняя стенка ХДФ 4 мм; фасады — МДФ, эмаль матовая 18 мм, цвет по колерной карте; столешница 38 мм, свес 20 мм; цоколь 100 мм.
3. Кромка: скрытые торцы 0,4 мм, видимые 2 мм. Номинальные зазоры: между фасадами 3 мм, фасад — столешница 3 мм, фасад — стена не менее 3 мм.
4. Ящики полного выдвижения и петли — с доводчиком; присадка по 32-й системе — выполняет цех.
5. Вытяжка встраивается в дно навесного модуля M_21 над варочной: её низ на 1550 мм от пола, 650 мм над панелью (не меньше 650 мм).
6. Ниши техники (холодильник — ориентир 1780 мм) — по монтажным схемам выбранных моделей: решётка в цоколе и канал за пеналом холодильника, зазор за духовым шкафом, фасад ПММ на двери машины.

					Проект: Квартира 103 м²	**M 1:20**
	Лист	№ док.	Подпись	Дата	Кухня (пом. 5). Развёртка гарнитура	Стадия / Лист / Листов
Дизайнер	Кырлан А.С.			04.11.26		П / Д_7 / 96

Ведомость отделки помещений (форма 1 прил. А ГОСТ 21.501-2018). Лист 1 из 2

№	Наименование помещения	Потолок			Стены и перегородки			Низ стен (плинтус)			Пол		Примечание
		Вид отделки	Код цвета	S, м²	Вид отделки	Код цвета	S, м²	Вид отделки	Код цвета	L, м	Вид отделки	S, м²	
1	Кабинет-библиотека 10,57 м²	ГКЛ по каркасу П113, отм. +2,550; окраска, Tikkurila Anti-Reflex 2, глубокоматовая, 2 слоя, подготовка Q3	NCS S 0502-Y	10,57	Окраска, Farrow & Ball Modern Emulsion, матовая, 2 слоя, подготовка Q3 Акцент — стена А: окраска, Farrow & Ball Modern Emulsion, матовая, 2 слоя, подготовка Q3	Farrow & Ball No. 291 Farrow & Ball No. 289	19,91 11,42	Плинтус МДФ h=83 мм, Ultrawood Base 5340, ЛДФ под окраску, 83×15 мм, 2440 мм (арт. LDF-BASE-5340)	Farrow & Ball No. 291	12,9	Инженерная доска, 1167-4250, 2100×127 мм, на клею; тип 1, отм. ЧП ±0,000	10,57	Н стен 2550 (до потолка); плинтус в цвет: стены
2	Кладовая 2,93 м²	Существующий потолок, отм. +2,650; окраска, Tikkurila Anti-Reflex 2, глубокоматовая, 2 слоя, подготовка Q3	NCS S 0502-Y	2,93	Окраска, Tikkurila Harmony, матовая, 2 слоя, подготовка Q3	NCS S 0502-Y	17,61	Плинтус МДФ h=83 мм, Ultrawood Base 5340, ЛДФ под окраску, 83×15 мм, 2440 мм (арт. LDF-BASE-5340)	NCS S 0502-Y	6,5	Инженерная доска, 1167-4250, 2100×127 мм, на клею; тип 1, отм. ЧП ±0,000	2,93	Н стен 2650 (до потолка); плинтус в цвет: стены
3	Гостиная-столовая 20,32 м²	ГКЛ по каркасу П113, отм. +2,550; окраска, Farrow & Ball Modern Emulsion, матовая, 2 слоя, подготовка Q3	Farrow & Ball No. 291	20,32	Окраска, Farrow & Ball Modern Emulsion, матовая, 2 слоя, подготовка К3 Акцент — стена А: окраска, Farrow & Ball Modern Emulsion, матовая, 3 слоя, аналог: интерьерная краска Farrow & Ball Modern Emulsion в цвете веера No. 255, матовая, подготовка К3	Farrow & Ball No. 291 Farrow & Ball No. 255	23,57 11,74	Плинтус МДФ h=83 мм, Ultrawood Base 5340, ЛДФ под окраску, 83×15 мм, 2440 мм (арт. LDF-BASE-5340)	Farrow & Ball No. 291	14,7	Инженерная доска, 1167-4250, 2100×127 мм, на клею; тип 2, отм. ЧП ±0,000	20,32	Н стен 2550 (до потолка); класс мокрого истирания по EN 13300 и блеск линейки Farrow & Ball Modern Emulsion — по ТУ производителя, в базе не сверены; потолок в цвет стен (No. 291) — краска бренда веера, Farrow & Ball Modern Emulsion; класс мокрого истирания по EN 13300 и блеск линейки Farrow & Ball Modern Emulsion — по ТУ производителя, в базе не сверены; колеруется в код стен, но по эмали на МДФ: сличать отдельным выкрасом на своей подложке (выкрас № 10); плинтус в цвет: стены
4	Прихожая-холл 12,91 м²	ГКЛ по каркасу П113, отм. +2,550; окраска, Tikkurila Anti-Reflex 2, глубокоматовая, 2 слоя, подготовка Q3	NCS S 0502-Y	12,91	Окраска, Farrow & Ball Modern Emulsion, матовая, 2 слоя, подготовка Q3	Farrow & Ball No. 291	33,88	Плинтус МДФ h=83 мм, Ultrawood Base 5340, ЛДФ под окраску, 83×15 мм, 2440 мм (арт. LDF-BASE-5340)	Farrow & Ball No. 291	12,6	Керамогранит, A8UZ, 600×1200×9 мм; тип 3, отм. ЧП ±0,000	12,91	Н стен 2550 (до потолка); матовая моющаяся, класс 1 EN 13300 — осознанно вместо полуматовой; плинтус в цвет: стены
5	Кухня 6,52 м²	ГКЛВ по каркасу П113, отм. +2,550; окраска, Farrow & Ball Modern Emulsion, матовая, 2 слоя, подготовка Q3	Farrow & Ball No. 291	6,52	Окраска, Farrow & Ball Modern Emulsion, матовая, 2 слоя, подготовка К3 Фартук кухни (стена Б, В): облицовка керамогранитом, аналог: керамогранит матовый, тон F497, 600×600×9 мм, клей C2 TE S1, затирка CG2WA	Farrow & Ball No. 291 #F1F1EC	20,51 2,01	Плинтус МДФ h=83 мм, Ultrawood Base 5340, ЛДФ под окраску, 83×15 мм, 2440 мм (арт. LDF-BASE-5340)	Farrow & Ball No. 291	9,4	Инженерная доска, 1167-4250, 2100×127 мм, на клею; тип 4, отм. ЧП ±0,000	6,52	Н стен 2550 (до потолка); моющаяся матовая окраска Farrow & Ball Modern Emulsion (краска бренда веера No. 291,); класс мокрого истирания по EN 13300 и блеск линейки Farrow & Ball Modern Emulsion — по ТУ производителя, в базе не сверены; категория К3 по СП 71.13330.2017, табл. 7.5; по ГКЛ каркаса П113, моющаяся окраска Farrow & Ball Modern Emulsion; Q3 класс мокрого истирания по EN 13300 и блеск линейки Farrow & Ball Modern Emulsion — по ТУ производителя, в базе не сверены; колеруется в код стен, но по эмали на МДФ: сличать отдельным выкрасом на своей подложке (выкрас № 10); плинтус в цвет: стены

Примечания

1. Ведомость продолжена на листе 2 из 2; итоги, сводка площадей и примечания — на последнем листе ведомости.

					Проект: Квартира 103 м²
	Лист	№ док.	Подпись	Дата	Ведомость отделки помещений. Лист 1 из 2
Дизайнер	Кырлан А.С.			04.11.26	

Стадия	Лист	Листов
П	С1	96

Ведомость отделки помещений (форма 1 прил. А ГОСТ 21.501-2018). Лист 2 из 2

№	Наименование помещения	Потолок			Стены и перегородки			Низ стен (плинтус)			Пол		Примечание
		Вид отделки	Код цвета	S, м²	Вид отделки	Код цвета	S, м²	Вид отделки	Код цвета	L, м	Вид отделки	S, м²	
6	Ванная 3,91 м²	ГКЛВ по каркасу П113, отм. +2,550; окраска, Tikkurila Luja 7, матовая, 2 слоя, подготовка Q3	NCS S 0502-Y	3,91	Облицовка плиткой, A8UZ, 600×1200×9 мм, клей C2 TE S1, затирка CG2WA	Atlas Concorde A8UZ	18,00	нет			Керамогранит, Atlas Concorde Marvel Travertine Sand CrossMatte Sensitech, арт. AFUL (той же коллекции, что стены A8UZ; тон сверить по образцу), 600×600×9 мм; тип 5, отм. ЧП −0,015	3,91	Н стен 2565 (до потолка); гидроизоляция обмазочная, 2 слоя, с заведением на стены 200 мм; над ванной — до 2000 и 300 мм за борт (по пирогу пола); тест проливом и акт скрытых работ
7	Постирочная 1,51 м²	Существующий потолок, отм. +2,650; окраска, Tikkurila Anti-Reflex 2, глубокоматовая, 2 слоя, подготовка Q3	NCS S 0502-Y	1,51	Окраска, Tikkurila Harmony, матовая, 2 слоя, подготовка Q3	NCS S 0502-Y	11,89	Плинтус МДФ h=83 мм, Ultrawood Base 5340, ЛДФ под окраску, 83×15 мм, 2440 мм (арт. LDF-BASE-5340)	NCS S 0502-Y	4,3	Инженерная доска, 1167-4250, 2100×127 мм, на клею; тип 1, отм. ЧП ±0,000	1,51	Н стен 2650 (до потолка); плинтус в цвет: стены
8	Спальня 2 11,42 м²	ГКЛ по каркасу П113, отм. +2,550; окраска, Tikkurila Anti-Reflex 2, глубокоматовая, 2 слоя, подготовка Q3	NCS S 0502-Y	11,42	Окраска, Farrow & Ball Modern Emulsion, матовая, 2 слоя, подготовка Q3 Акцент — стена А: окраска, Farrow & Ball Modern Emulsion, матовая, 2 слоя, подготовка Q3	Farrow & Ball No. 291 Farrow & Ball No. 289	20,89 12,09	Плинтус МДФ h=83 мм, Ultrawood Base 5340, ЛДФ под окраску, 83×15 мм, 2440 мм (арт. LDF-BASE-5340)	Farrow & Ball No. 291	13,6	Инженерная доска, 1167-4250, 2100×127 мм, на клею; тип 1, отм. ЧП ±0,000	11,42	Н стен 2550 (до потолка); плинтус в цвет: стены
9	Коридор 6,02 м²	ГКЛ по каркасу П113, отм. +2,550; окраска, Tikkurila Anti-Reflex 2, глубокоматовая, 2 слоя, подготовка Q3	NCS S 0502-Y	6,02	Окраска, Farrow & Ball Modern Emulsion, матовая, 2 слоя, подготовка Q3	Farrow & Ball No. 291	29,17	Плинтус МДФ h=83 мм, Ultrawood Base 5340, ЛДФ под окраску, 83×15 мм, 2440 мм (арт. LDF-BASE-5340)	Farrow & Ball No. 291	10,8	Инженерная доска, 1167-4250, 2100×127 мм, на клею; тип 1, отм. ЧП ±0,000	6,02	Н стен 2550 (до потолка); матовая моющаяся, класс 1 EN 13300 — осознанно вместо полуматовой; плинтус в цвет: стены
10	Спальня мастер 22,48 м²	ГКЛ по каркасу П113, отм. +2,550; окраска, Tikkurila Anti-Reflex 2, глубокоматовая, 2 слоя, подготовка Q3	NCS S 0502-Y	22,48	Окраска, Farrow & Ball Modern Emulsion, матовая, 2 слоя, подготовка Q3 Акцент — стена А: окраска, Farrow & Ball Modern Emulsion, матовая, 2 слоя, подготовка Q3	Farrow & Ball No. 291 Farrow & Ball No. 289	31,48 12,09	Плинтус МДФ h=83 мм, Ultrawood Base 5340, ЛДФ под окраску, 83×15 мм, 2440 мм (арт. LDF-BASE-5340)	Farrow & Ball No. 291	18,5	Инженерная доска, 1167-4250, 2100×127 мм, на клею; тип 1, отм. ЧП ±0,000	22,48	Н стен 2550 (до потолка); плинтус в цвет: стены
11	Ванная мастер 2,13 м²	ГКЛВ по каркасу П113, отм. +2,550; окраска, Tikkurila Luja 7, матовая, 2 слоя, подготовка Q3	NCS S 0502-Y	2,13	Облицовка плиткой, A8UZ, 600×1200×9 мм, клей C2 TE S1, затирка CG2WA	Atlas Concorde A8UZ	12,57	нет			Керамогранит, Atlas Concorde Marvel Travertine Sand CrossMatte Sensitech, арт. AFUL (той же коллекции, что стены A8UZ; тон сверить по образцу), 600×600×9 мм; тип 5, отм. ЧП −0,015	2,13	Н стен 2565 (до потолка); гидроизоляция обмазочная, 2 слоя, с заведением на стены 200 мм; у душа — до 2000 и 500 мм за поддон (по пирогу пола); тест проливом и акт скрытых работ
	Итого			**100,72**			**288,83**			**103,5**		**100,72**	

Примечания

1. Площади поверхностей — по чистым граням стен до отделки: стены = периметр × высоту от чистого пола помещения до низа потолка минус проёмы (облицовка плиткой — до верха облицовки); плинтус = периметр минус дверные проёмы; пол и потолок — по площади помещения. Количество плиток по раскладке. Площади помещений — с учётом всех частей помещения; откосы в площадь стен не входят.
2. Акцентные стены и фартук — отдельными строками, их площадь вычтена из основной отделки стен помещения; фартук — над нижними модулями кухни от столешницы до низа навесных шкафов, где шкафов нет — на 600 мм.
3. Плинтус — длина по периметру за вычетом дверных проёмов; примыкания к наличникам и встроенной мебели — по развёрткам.
4. Формат плитки — Ш×В×Т (ширина × высота в положении укладки × толщина), мм; на полу — вдоль стен А/В × вдоль стен Б/Г.
5. Коды цвета — по веерам производителей; колеровка каждой краски одной партией, проверка выкраса при свете D65 и при лампах проекта.
6. Уровни подготовки Q1–Q4 — система Knauf, не норма ГОСТ/СП; допуски поверхностей — по СП 71.13330.2017 (действующая редакция).
7. «аналог:» — изделие задано характеристиками, марку и артикул согласовать с заказчиком до закупки.
8. Плавающая стяжка по звукоизоляции: демпферная (кромочная) лента по контуру помещения и у стояков (СП 51.13330.2011, п. 9.11); плинтус крепится только к стене.
9. Сводка площадей по материалам, м²: потолок — NCS S 0502-Y Anti-Reflex 2 — 67,84; потолок — Farrow & Ball No. 291 Modern Emulsion — 26,84; потолок — NCS S 0502-Y Luja 7 — 6,04; стены — Farrow & Ball No. 291 Modern Emulsion — 179,41; стены — Farrow & Ball No. 289 Modern Emulsion 35,60; стены — NCS S 0502-Y Harmony — 29,50; стены — Farrow & Ball No. 255 Modern Emulsion — 11,74; стены — облицовка плиткой 600×1200×9 мм, Atlas Concorde A8UZ — 30,57; фартук — облицовка керамогранитом, #F1F1EC — 2,01.

					Проект: Квартира 103 м²
	Лист	№ док.	Подпись	Дата	Ведомость отделки помещений. Лист 2 из 2
Дизайнер	Кырлан А.С.			04.11.26	

Стадия	Лист	Листов
П	С2	96

Поз.	Наименование и техническая характеристика	Тип, марка, обозначение документа	Код продукции	Поставщик	Ед. изм.	Кол.	Образец	Примечание
	Лакокрасочные материалы							
1	Краска интерьерная водно-дисперсионная акриловая для стен и потолков, матовая, класс мокрого истирания 1 по EN 13300, база A; цвет по вееру Farrow & Ball No. 291 «School House White — тёплый меловой белый», колеровка машинная	Farrow & Ball Modern Emulsion		Farrow & Ball	л	55		поз. К1 колерной карты; пом. 1, 3, 4, 5, 8, 9, 10; S = 206,3 м² × 2 сл. × 0,12 л/м² = 49,5 л, +10 % и 0,5 л на подкраску → ≥ 55,0 л; тара 11 × 5 л
2	Краска интерьерная водно-дисперсионная акриловая для акцентных стен, матовая, класс мокрого истирания 1 по EN 13300, база C; цвет по вееру Farrow & Ball No. 289 «Inchyra Blue — тёмный сине-серый», колеровка машинная	Farrow & Ball Modern Emulsion		Farrow & Ball	л	10		поз. К2 колерной карты; пом. 1, 8, 10; S = 35,6 м² × 2 сл. × 0,12 л/м² = 8,5 л, +10 % и 0,5 л на подкраску → ≥ 9,9 л; тара 2 × 5 л
3	Краска интерьерная водно-дисперсионная акриловая для потолков, глубокоматовая, класс мокрого истирания 2 по EN 13300, база A; цвет NCS S 0502-Y «Белый с лёгкой желтизной», колеровка машинная	Tikkurila Anti-Reflex 2		Tikkurila	л	18,9		поз. К3 колерной карты; пом. 1, 2, 4, 7, 8, 9, 10; S = 67,8 м² × 2 сл. × 0,12 л/м² = 16,3 л, +10 % и 0,5 л на подкраску → ≥ 18,4 л; тара 2 × 9 л + 1 × 0,9 л
4	Краска интерьерная водно-дисперсионная акриловая для стен, матовая, класс мокрого истирания 1 по EN 13300, база A; цвет NCS S 0502-Y «Белый с лёгкой желтизной», колеровка машинная	Tikkurila Harmony		Tikkurila	л	9		поз. К5 колерной карты; пом. 2, 7; S = 29,5 м² × 2 сл. × 0,12 л/м² = 7,1 л, +10 % и 0,5 л на подкраску → ≥ 8,3 л; тара 1 × 9 л
5	Краска интерьерная водно-дисперсионная акриловая для акцентных стен, матовая, класс мокрого истирания 1 по EN 13300, база C; цвет по вееру Farrow & Ball No. 255 «Tanner's Brown — тёмный шоколад», колеровка машинная	Farrow & Ball Modern Emulsion		Farrow & Ball	л	7,5		поз. К7 колерной карты; пом. 3; S = 11,7 м² × 3 сл. × 0,12 л/м² = 4,2 л, +10 % и 0,5 л на подкраску → ≥ 5,1 л; тара 1 × 5 л + 1 × 2,5 л
6	Краска интерьерная водно-дисперсионная акриловая для потолков, матовая, класс мокрого истирания 1 по EN 13300, база A; цвет NCS S 0502-Y «Белый с лёгкой желтизной», колеровка машинная	Tikkurila Luja 7		Tikkurila	л	2,7		поз. К9 колерной карты; пом. 6, 11; S = 6,0 м² × 2 сл. × 0,12 л/м² = 1,4 л, +10 % и 0,5 л на подкраску → ≥ 2,1 л; тара 1 × 2,7 л
7	Краска для МДФ и дерева в цвет Farrow & Ball No. 291 «School House White — тёплый меловой белый» — окраска плинтуса; блеск не ниже блеска стен	марка не задана			л	2,4		поз. К4, К8; пом. 1, 3, 4, 5, 8, 9, 10; L = 92,6 м, S = 9,1 м² × 2 сл. × 0,12 л/м² + 10 %; продукт подобрать в веере Farrow & Ball
8	Краска для МДФ и дерева в цвет NCS S 0502-Y «Белый с лёгкой желтизной» — окраска плинтуса; блеск не ниже блеска стен	марка не задана			л	0,5		поз. К6; пом. 2, 7; L = 10,8 м, S = 1,1 м² × 2 сл. × 0,12 л/м² + 10 %; продукт подобрать в веере NCS
9	Грунтовка акриловая под окраску стен и потолков — из системы производителя краски	по системе краски			м²	357		площадь окраски стен, акцентов и потолков; 1 слой перед окраской; расход — по ТУ грунтовки
	Плитка и керамогранит							
10	Atlas Concorde Marvel Travertine Sand Cross 60×60 Matte Sensitech, арт. AFUL (той же коллекции, что стены A8UZ; тон сверить по образцу), 600×600×9 мм, ректификат, водопоглощение 0,1 % (BIa), противоскольжение R10, PEI IV	Atlas Concorde Marvel Travertine Sand Cross 60×60 Matte Sensitech, арт. AFUL (той же коллекции, что стены A8UZ; тон сверить по образцу)			м²	9,36		шов 2 мм; Ванная, пол; Ванная мастер, пол; по раскладке 23 шт (S = 6,04 м²), с запасом 26 шт
11	A8UZ, 600×1200×9 мм, ректификат, водопоглощение 0,1 % (BIa), противоскольжение R10, PEI IV	A8UZ		Atlas Concorde	м²	70,56		шов 2 мм; Ванная, стены А–Г; Ванная, короб инсталляции; Ванная мастер, стены А–Г; Ванная мастер, короб инсталляции; Прихожая-холл, пол; по раскладке 86 шт (S = 45,03 м²), с запасом 98 шт
12	Керамогранит матовый, тон F497, ректификат, водопоглощение 0,5 % (BIa)	аналог по характеристикам			м²	2,22		5. Кухня, фартук; раскладка не выполнена — S = 2,01 м² + 10 %; клей и затирка — по раскладке
	Напольные покрытия							
13	1167-4250, рабочий слой 4 мм, эмиссия E1, укладка на клей	1167-4250		Coswick	м²	87,5		пом. 1, 2, 3, 5, 7, 8, 9, 10; S = 81,77 м² + 7 % (прямая укладка); к заказу — кратно упаковке
14	Клей для паркета и инженерной доски, эластичный (СМП / полиуретановый)	по рекомендации производителя доски			м²	82		площадь приклейки; расход и шпатель — по ТУ клея
	Погонажные изделия							
15	Ultrawood Base 5340, ЛДФ под окраску, 83×15 мм, 2440 мм (арт. LDF-BASE-5340), крепление к стене, окраска в цвет Farrow & Ball No. 291	Ultrawood Base 5340, ЛДФ под окраску, 83×15 мм, 2440 мм (арт. LDF-BASE-5340)			м	102		пом. 1, 3, 4, 5, 8, 9, 10; L = 92,6 м (периметр без дверных проёмов) + 10 % на подрезку; в штуках — по длине планки
16	Ultrawood Base 5340, ЛДФ под окраску, 83×15 мм, 2440 мм (арт. LDF-BASE-5340), крепление к стене, окраска в цвет NCS S 0502-Y	Ultrawood Base 5340, ЛДФ под окраску, 83×15 мм, 2440 мм (арт. LDF-BASE-5340)			м	12		пом. 2, 7; L = 10,8 м (периметр без дверных проёмов) + 10 % на подрезку; в штуках — по длине планки
	Смеси и материалы для облицовки							
17	Затирка для швов плитки, класс CG2WA по EN 13888	Mapei Ultracolor Plus 132		Mapei	кг	4		по раскладке (a+b)/(a·b) × шов × t × 1,6 + 10 %; в т. ч. 1,0 кг — позиции раскладки без марки
18	Клей плиточный C2 TE S1 по EN 12004, слой 5 мм	Ceresit CM 17		Ceresit	кг	402		17 меш. по 25 кг; 1,5 кг/м² на 1 мм слоя + 10 %; в т. ч. 105 кг — позиции раскладки без марки
19	Гидроизоляция обмазочная мокрых зон: пол, стены по периметру, зоны замачивания; 2 слоя с армирующей лентой в углах	аналог по характеристикам			м²	18,7		площадь по листу раскладки плитки + 10 %; расход смеси — по ТУ
20	Лента демпферная по периметру пола из плитки	аналог по характеристикам			м	27,1		периметр без дверных проёмов + 10 %

Примечания

1. Количества — из геометрии проекта: площади поверхностей по чистым граням стен до отделки (те же, что в ведомости отделки и колерной карте), плитка, клей и затирка — по раскладке плиточника; в графе «Кол.» — к заказу, с запасом.
2. Краска: расход 0,12 л/м² на слой в 2 слоя, если по ТУ не задан иной; запас 10 % и 0,5 л на подкраску каждого кода. Один код — одна партия, колеровка машинная в колеровочном центре бренда; в заказ — только после утверждения выкраса (колерная карта). Фасовка — по каталогу бренда на дату выпуска; к заказу — не меньше расчётного объёма.
3. «Аналог по характеристикам» — допускается изделие другого производителя с характеристиками не ниже указанных, по согласованию с автором проекта.
4. Графы «Код продукции» и «Масса 1 ед.» не заполнены: коды по классификатору продукции не присвоены, масса единицы до 25 кг (ГОСТ 21.110-2013).
5. Грунтовка и клей для доски указаны площадью обработки; объём — по ТУ выбранного продукта.

	Лист	№ док.	Подпись	Дата	Проект: Квартира 103 м²
Дизайнер	Кырлан А.С.			04.11.26	Спецификация отделочных материалов

Стадия	Лист	Листов
П	С3	96

Список покупок: материалы для магазина

№	Что купить	Артикул или характеристика	Нужно с запасом	Брать в магазине	Фасовка	Уточнить в магазине	Помещения	Кто покупает
Покрытия полов и облицовка								
1	Инженерная доска (дуб натуральный, рабочий слой 4 мм, эмиссия E1, прямая укладка)	1167-4250	88,3 м²	88,3 м²		уточнить в магазине: м² в упаковке	1, 2, 3, 5, 7, 8, 9, 10	по проекту
2	Клей для паркетной и инженерной доски (эластичный, по ТУ изготовителя доски)	на выбор бригады по проекту	82,52 м²			уточнить в магазине: расход и фасовку — по выбранному продукту		бригада
3	Керамогранит 600×600 мм Atlas Concorde Marvel Travertine Sand Cross 60×60 Matte Sensitech, арт. AFUL (той же коллекции, что стены A8UZ; тон сверить по образцу)	Atlas Concorde Marvel Travertine Sand Cross 60×60 Matte Sensitech, арт. AFUL (той же коллекции, что стены A8UZ; тон сверить по образцу)	26 шт	26 шт		уточнить в магазине: штук в коробке	6, 11	по проекту
4	Керамогранит 600×1200 мм A8UZ	A8UZ	95 шт	98 шт		уточнить в магазине: штук в коробке	4, 6, 11	по проекту
Сухие смеси и гидроизоляция								
5	Клей плиточный цементный класса C2 TE S1 (ГОСТ Р 56387-2018)	Ceresit CM 17 или аналог	401,01 кг	17 меш.	мешок 25 кг			по проекту
6	Затирка цементная класса CG2WA, цвет — по колерной карте	Mapei Ultracolor Plus 132 или аналог	3,97 кг	2 упак.	упак. 2 кг			по проекту
7	Гидроизоляция обмазочная полимерная, 2 слоя, лента в углах, манжеты на выводах	на выбор бригады по проекту	18,71 м²			уточнить в магазине: расход и фасовку — по выбранному продукту	6, 11	бригада
8	Лента демпферная по периметру пола из плитки	на выбор бригады по проекту	27,15 м	28 м		уточнить в магазине: фасовку		бригада
9	Смесь цементно-песчаная для стяжки М200 (50 мм, 49 мм, 47 мм, 33 мм)	на выбор бригады по проекту	5,2 м³			уточнить в магазине: расход и фасовку — по выбранному продукту		бригада
10	Смесь штукатурная гипсовая для машинного и ручного нанесения по маякам, слой до 10 мм	на выбор бригады по проекту	320,19 м²			уточнить в магазине: расход и фасовку — по выбранному продукту	1, 2, 3, 4, 5, 6, 7, 8, 9, 10, 11	бригада
Короба из ГКЛВ								
11	Лист ГКЛВ 12,5 мм, 2500 × 1200 мм, обшивка коробов в 2 слоя	на выбор бригады по проекту	7,11 м²	3 лист.	лист 3,00 м²		6, 11	бригада
12	Профиль стальной оцинкованный 27 × 28 мм: каркас коробов (стойки и направляющие)	на выбор бригады по проекту	17,16 м	6 шт	хлыст 3 м			бригада
Слаботочные сети								
13	Кабель домофона — тип по системе поставщика	на выбор бригады по проекту	4,3 м	5 м		уточнить в магазине: длину бухты		бригада
14	Кабель коаксиальный RG-6 (75 Ом) к розеткам ТВ	на выбор бригады по проекту	16,1 м	17 м		уточнить в магазине: длину бухты		бригада
15	Кабель U/UTP кат. 6 (LAN, Wi-Fi и камеры по PoE)	на выбор бригады по проекту	70,3 м	71 м		уточнить в магазине: длину бухты		бригада
16	Гофротруба Ø20 для слаботочных линий, отдельно от силовых	на выбор бригады по проекту	81,6 м	82 м		уточнить в магазине: длину бухты		бригада
17	Розетка компьютерная RJ45, кат. 6, с рамкой и подрозетником	на выбор бригады по проекту	4 шт	4 шт	шт			бригада
18	Розетка телевизионная (коаксиальная) с рамкой и подрозетником	на выбор бригады по проекту	1 шт	1 шт	шт			бригада

					Проект: Квартира 103 м²	
	Лист	№ док.	Подпись	Дата	Список покупок	Стадия / Лист / Листов
Дизайнер	Кырлан А.С.			04.11.26		П / С4 / 96

Список покупок: материалы для магазина (продолжение)

№	Что купить	Артикул или характеристика	Нужно с запасом	Брать в магазине	Фасовка	Уточнить в магазине	Помещения	Кто покупает
19	Трубка или монитор домофона (поставка домофонной организации)	на выбор бригады по проекту	1 шт	1 шт	шт			по проекту
20	Щит слаботочный ЩС: корпус, DIN-рейка, розетки 220 В	на выбор бригады по проекту	1 шт	1 шт	шт			бригада
21	Патч-панель, портов не менее 5	на выбор бригады по проекту	1 шт	1 шт	шт			бригада
Лакокрасочные материалы								
22	Краска интерьерная акриловая, матовая, класс истирания 1	Farrow & Ball Modern Emulsion No. 289 «Inchyra Blue — тёмный сине-серый»	9,39 л	4 банк.	банка 2,5 л		1, 8, 10	по проекту
23	Краска интерьерная акриловая, матовая, класс истирания 1	Farrow & Ball Modern Emulsion No. 291 «School House White тёплый меловой белый»	54,98 л	22 банк.	банка 2,5 л		1, 3, 4, 5, 8, 9, 10	по проекту
24	Краска интерьерная акриловая, глубокоматовая, класс истирания 2	Tikkurila Anti-Reflex 2 S 0502-Y «Белый с лёгкой желтизной»	17,91 л	7 банк.	банка 2,7 л		1, 2, 4, 7, 8, 9, 10	по проекту
25	Краска интерьерная акриловая, матовая, класс истирания 1	Tikkurila Harmony S 0502-Y «Белый с лёгкой желтизной»	7,79 л	3 банк.	банка 2,7 л		2, 7	по проекту
26	Краска интерьерная акриловая, матовая, класс истирания 1	Farrow & Ball Modern Emulsion No. 255 «Tanner's Brown — тёмный шоколад»	4,65 л	2 банк.	банка 2,5 л		3	по проекту
27	Краска интерьерная акриловая, матовая, класс истирания 1	Tikkurila Luja 7 S 0502-Y «Белый с лёгкой желтизной»	1,6 л	1 банк.	банка 2,7 л		6, 11	по проекту
28	Шпаклёвка финишная полимерная под окраску (стены и потолки, Q3)	на выбор бригады по проекту	394,88 м²			уточнить в магазине: расход и фасовку — по выбранному продукту		бригада
29	Грунтовка акриловая глубокого проникновения, 2 слоя	на выбор бригады по проекту	430,98 м²			уточнить в магазине: расход и фасовку — по выбранному продукту		бригада
Погонажные изделия и потолки								
30	Плинтус напольный МДФ под покраску, h=83 мм, крепление к стене	Ultrawood Base 5340, ЛДФ под окраску, 83×15 мм, 2440 мм (арт. LDF-BASE-5340)	113,83 м.п.	48 шт	хлыст 2,4 м		1, 2, 3, 4, 5, 7, 8, 9, 10	по проекту
31	Потолок подвесной ГКЛ/ГКЛВ по каркасу Knauf П113: листы, профили, подвесы, лента, шпаклёвка швов	Knauf П113	96,28 м²			уточнить в магазине: расход и фасовку — по выбранному продукту		по проекту

Примечания


1. «Нужно с запасом» — расход по чертежам и раскладке плюс запас на подрезку и подкраску; «Брать в магазине» — то же количество в единицах, которыми продают (банки, мешки, упаковки, листы, штуки, литры).
2. «Уточнить в магазине» — фасовки этого товара в проекте нет: спросите у продавца, сколько в упаковке, и возьмите целое число упаковок не меньше «Нужно с запасом».
3. Плитку, доску и краску одного цвета берите одной партией (один калибр и тон на помещение) и сохраните чек и номер партии до конца ремонта.
4. «По характеристике» — артикул не выбран: подойдёт любой товар с этими свойствами, согласуйте его с дизайнером до покупки. «Бригада» материал выбирает и закупает бригада по своей технологии.
5. Помещения: 1 — Кабинет-библиотека; 2 — Кладовая; 3 — Гостиная-столовая; 4 — Прихожая-холл; 5 — Кухня; 6 — Ванная; 7 — Постирочная; 8 Спальня 2; 9 — Коридор; 10 — Спальня мастер; 11 — Ванная мастер; «—» — материал для нескольких помещений, расход по месту.

					Проект: Квартира 103 м²
	Лист	№ док.	Подпись	Дата	
Дизайнер	Кырлан А.С.			04.11.26	Список покупок (окончание)

Стадия	Лист	Листов
П	С5	96


1 Порог 15 мм: мокрая зона — смежное помещение (М 1:10)

Применение: двери Д-5, Д-9

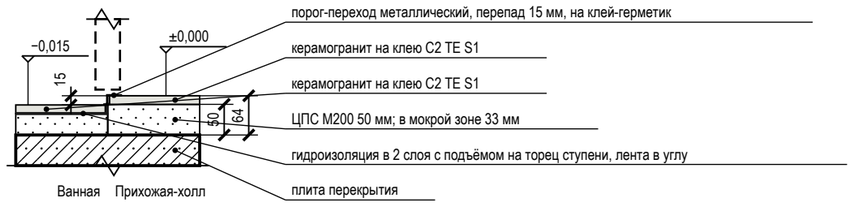


2 Дверь скрытого монтажа в плоскости стены, плинтус (М 1:5)

Применение: двери Д-2, Д-3, Д-4, Д-5, Д-6, Д-7, Д-8, Д-9

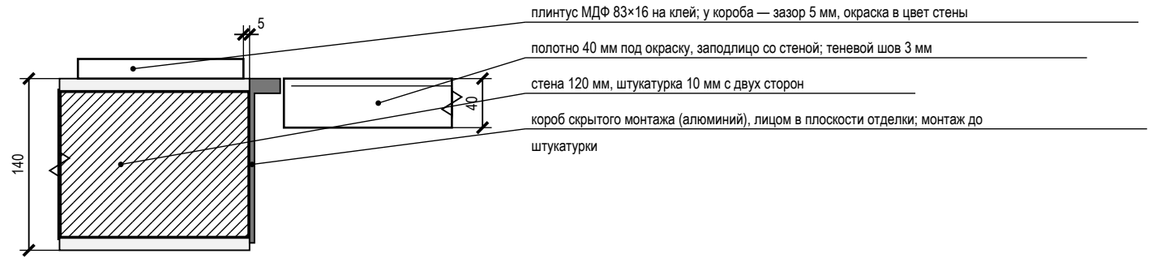


3 Короб стояков К1-1, К1-2 (кухня) с люком и звукоизоляцией (М 1:10)

Применение: пом. 6, 5, 11, 7

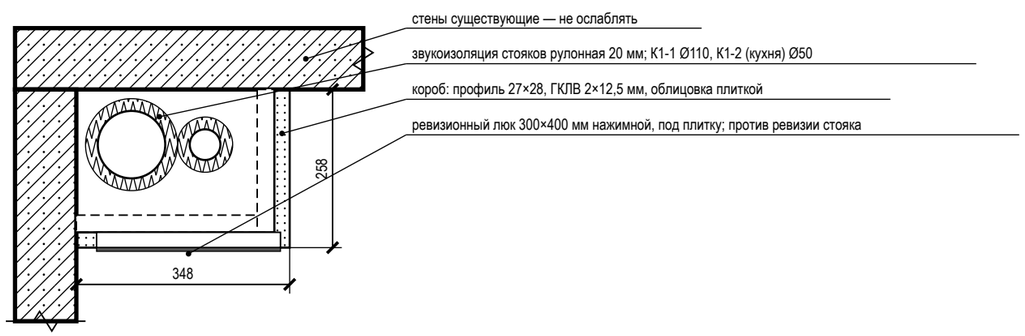


4 Гидроизоляция санузла: заход на стены 200 мм, примыкание ванны (М 1:20)

Применение: пом. 6, 11

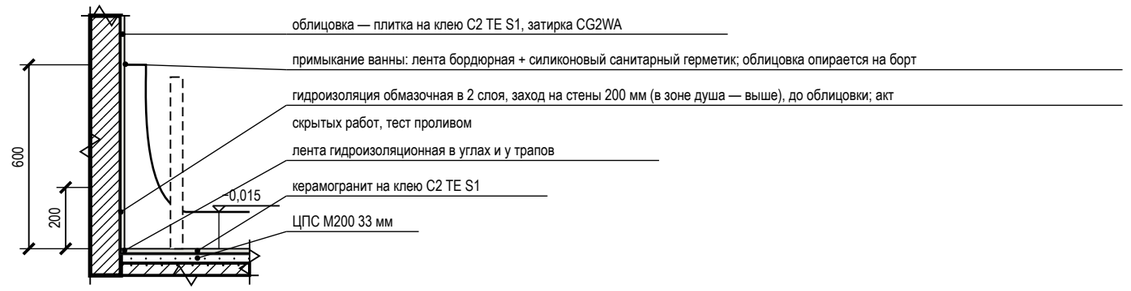


5 Плинтус МДФ 83×15 мм у окрашенной стены по доске (ламинату) (М 1:10)

Применение: пом. 1, 2, 3, 5, 7, 8, 9, 10

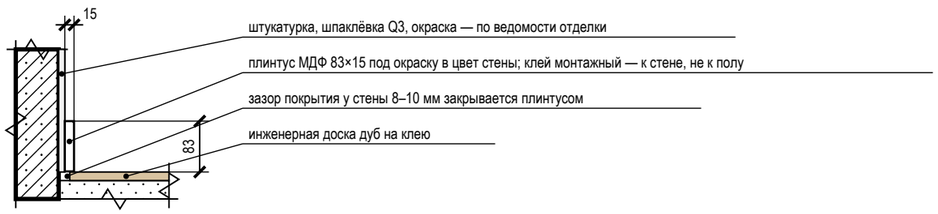

6 Плинтус МДФ 83×15 мм у окрашенной стены по керамограниту (плитке) (М 1:10)

Применение: пом. 4

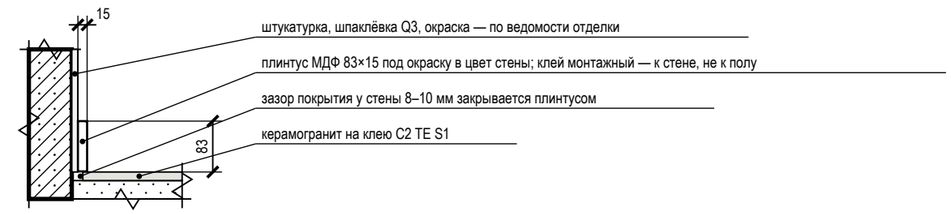

Условные обозначения

- железобетон (плита, стены) — условно: конструкция не установлена
- кладка, перегородка — условно: конструкция не установлена
- стяжка, раствор
- гипсокартон ГКЛВ
- звукоизоляция, эластичный заполнитель
- плитка, керамогранит на клею
- инженерная доска (покрытие пола)
- металлический профиль (порог, Т-профиль, короб двери)
- гидроизоляция (обмазочная, лента)

Примечания

1. Узлы — типовые решения проекта для мест, отмеченных выносками на листе схемы расположения развёрток и узлов; размеры — в мм, отметки — в м от ±0,000.
2. Узлы с гидроизоляцией, закладными и коробами скрытого монтажа принимаются по актам скрытых работ до закрытия отделкой; гидроизоляция — после теста проливом (24 ч).
3. Марки изделий (порог, Т-профиль, короб скрытой двери, люк) — по спецификациям; замена — на аналог с теми же габаритами по согласованию с автором проекта.
4. Материал плиты перекрытия и стен в узлах показан условно (железобетон, кладка): конструкция дома не установлена — крепёж, анкеры и толщины слоёв уточняются после обследования (до него — по допущениям общих указаний).

					Проект: Квартира 103 м²
	Лист	№ док.	Подпись	Дата	Узлы
Дизайнер	Кырлан А.С.			04.11.26	

Стадия	Лист	Листов
П	С6	96

выпуск 04.11.2026 № d6a6e5e88d · стр. 96 из 96