ДИЗАЙН-ПРОЕКТ ИНТЕРЬЕРА

Квартира 58 м²

кухня-гостиная и спальня

55,23 м²

светло · спокойно · уютно (hygge) · естественно · функционально · в меру (lagom)

Палитра из: тёплые нейтрали NCS (стены по ведомости — S 1002-Y50R / S 1502-Y50R близки к ним), акцент — пыльный синий в текстиле.

ПАЛИТРА 60 / 30 / 10

NCS S 0500-N	NCS S 1500-N	NCS S 2002-Y	NCS S 4010-R90B
60 %	30 %	30 %	10 %

АВТОР ПРОЕКТА

Кырлан Александр Сергеевич

Октябрь 2026

место под визуализацию: вид сверху (3D) с мебелью, текстилем и декором

Визуализация «вид сверху» — в работе

ОБЪЕКТ	ОБЩАЯ ПЛОЩАДЬ	ПОМЕЩЕНИЙ
Квартира 58 м²	55,23 м²	6, из них жилых 2

СТИЛЬ	СТАДИЯ	ШИФР
Скандинавский · кухня-гостиная и спальня	Рабочий проект	ГД-2026-006-АИ

КАК ОСТАВИТЬ ПРАВКУ

Нажмите кнопку «Правка к этому листу» в правом верхнем углу любого листа — лист откроется на сайте студии: отметьте место на чертеже и наговорите замечание голосом или напишите текстом.

Или откройте все листы проекта:

alex1986-rgb.github.io/linea-design-studio/review.html?p=gost-kv58

					Проект: Квартира 58 м²			
	Лист	№ док.	Подпись	Дата	Титульный лист	Стадия	Лист	Листов
Дизайнер	Кырлан А.С.			09.10.26		П	1	60

выпуск 09.10.2026 · 7efd137e8f · стр. 1 из 60

Правка к этому листу

Список листов

Лист	Наименование
1	Титульный лист
2	Список листов
3	План планировки от заказчика
4	План монтажный
5	Кухня (пом. 1). Монтажная схема
6	Шкафы. Монтажная схема
7	Карта покрытий стен
8	Колерная карта
9	План размещения мебели и оборудования
10	Спецификация мебели и оборудования
11	Ведомости изделий, техники и фурнитуры
12	План выводов сантехники
13	Схема разводки водопровода и канализации
14	Спецификация сантехнического оборудования
15	План размещения дверей
16	План потолков
17	План розеток и электровыводов
18	План слаботочных сетей
19	План освещения
20	Спецификация светильников и сценарии освещения
21	Управление светильниками
22	План вентиляции
23	План отопления
24	План покрытий пола
25	Раскладка плитки. Планы полов
26	Раскладка плитки. Ванная. Санузел. Прихожая
27	Визуализация кухни-гостиной
28	Визуализация кухни-гостиной
29	Визуализация кухни-гостиной
30	Развёртка стены В. Кухня-гостиная (пом. 1), кухонный фронт
31	Развёртка стены А. Кухня-гостиная (пом. 1)
32	Развёртка стены Б. Кухня-гостиная (пом. 1)
33	Развёртка стены Г. Кухня-гостиная (пом. 1)
34	Визуализация спальни
35	Визуализация спальни
36	Развёртка стены А. Спальня (пом. 2)
37	Развёртка стены Б. Спальня (пом. 2)
38	Развёртка стены В. Спальня (пом. 2)
39	Визуализация ванной
40	Визуализация ванной

Лист	Наименование
41	Развёртки стен А, Б. Ванная (пом. 3)
42	Развёртки стен В, Г. Ванная (пом. 3)
43	Визуализация санузла
44	Развёртки стен А, Б. Санузел (пом. 4)
45	Развёртки стен В, Г. Санузел (пом. 4)
46	Визуализация прихожей
47	Визуализация прихожей
48	Развёртка стены А. Прихожая (пом. 5)
49	Развёртка стены Б. Прихожая (пом. 5)
50	Развёртка стены В. Прихожая (пом. 5)
51	Развёртка стены Г. Прихожая (пом. 5)
52	Визуализация гардеробной
53	Развёртки стен А, Б. Гардеробная (пом. 6)
54	Развёртка стены Г. Гардеробная (пом. 6)
Д_1	Шкаф-купе М_13
Д_2	Система хранения М_14
Д_3	Кухня (пом. 1). Развёртка гарнитура
С1	Ведомость отделки помещений
С2	Спецификация отделочных материалов
С3	Узлы


Общие указания

1. Размеры даны в мм от чистовых поверхностей стен: слой штукатурки 20 мм по блоку и 5 мм шпаклёвки по ГКЛ учтён. Перед заказом встроенной мебели — контрольный обмер после штукатурки.
2. Привязки мебели — от стен и углов помещения, а не от другой мебели.
3. Розетки, выводы и выключатели под мебель — см. лист 17 «План розеток и электровыводов»; сантехприборы и выводы воды — лист 12.
4. План расстановки не является документацией для изготовления мебели: изделия — по чертежам мебельщика; покупную мебель заменять только на изделия не больше габарита из спецификации (лист 10).
5. Встроенная мебель «стена в стену» — с зазором 10 мм с каждой стороны или с компенсаторами.
6. Развёртки — вид на стену изнутри помещения, по часовой стрелке; расположение стен на схеме листа развёртки; размеры — в мм по чистовым поверхностям; отметки — в м от ±0,000; высоты Н — от чистого пола помещения до оси изделия, у декора — до центра.
7. Красные цепочки — привязки электроточек и выводов: по горизонтали от угла чистовых стен, по вертикали от чистого пола, до оси изделия; звенья короче 3 мм на листе вынесены во второй ярус (ближняя к стене цепочка).
8. У знака электроточки: марка (Р — розетка, S — выключатель, Св — светильник, ЭВ вывод кабеля), ×N — число постов в рамке, гр. — группа щита, Н — высота оси от чистого пола, мм; группы по клавишам выключателя — на листе выключателей.
9. Схема мебели, приборов и декора не является технической документацией для производства мебели; габариты — по паспортам изделий.
10. Марки позиций: М_NN — мебель, ОБ_NN — оборудование, С_NN — сантехника; О-N отделка (ведомость отделочных материалов, серия С).
11. Размеры мебели и изделий на заказ уточнить по месту после отделочных работ.

					Проект: Квартира 58 м²
	Лист	№ док.	Подпись	Дата	
Дизайнер	Кырлан А.С.			09.10.26	Список листов
					Стадия: П; Лист: 2; Листов: 60

выпуск 09.10.2026 № 7efd137e8f · стр. 2 из 60

Правка к этому листу

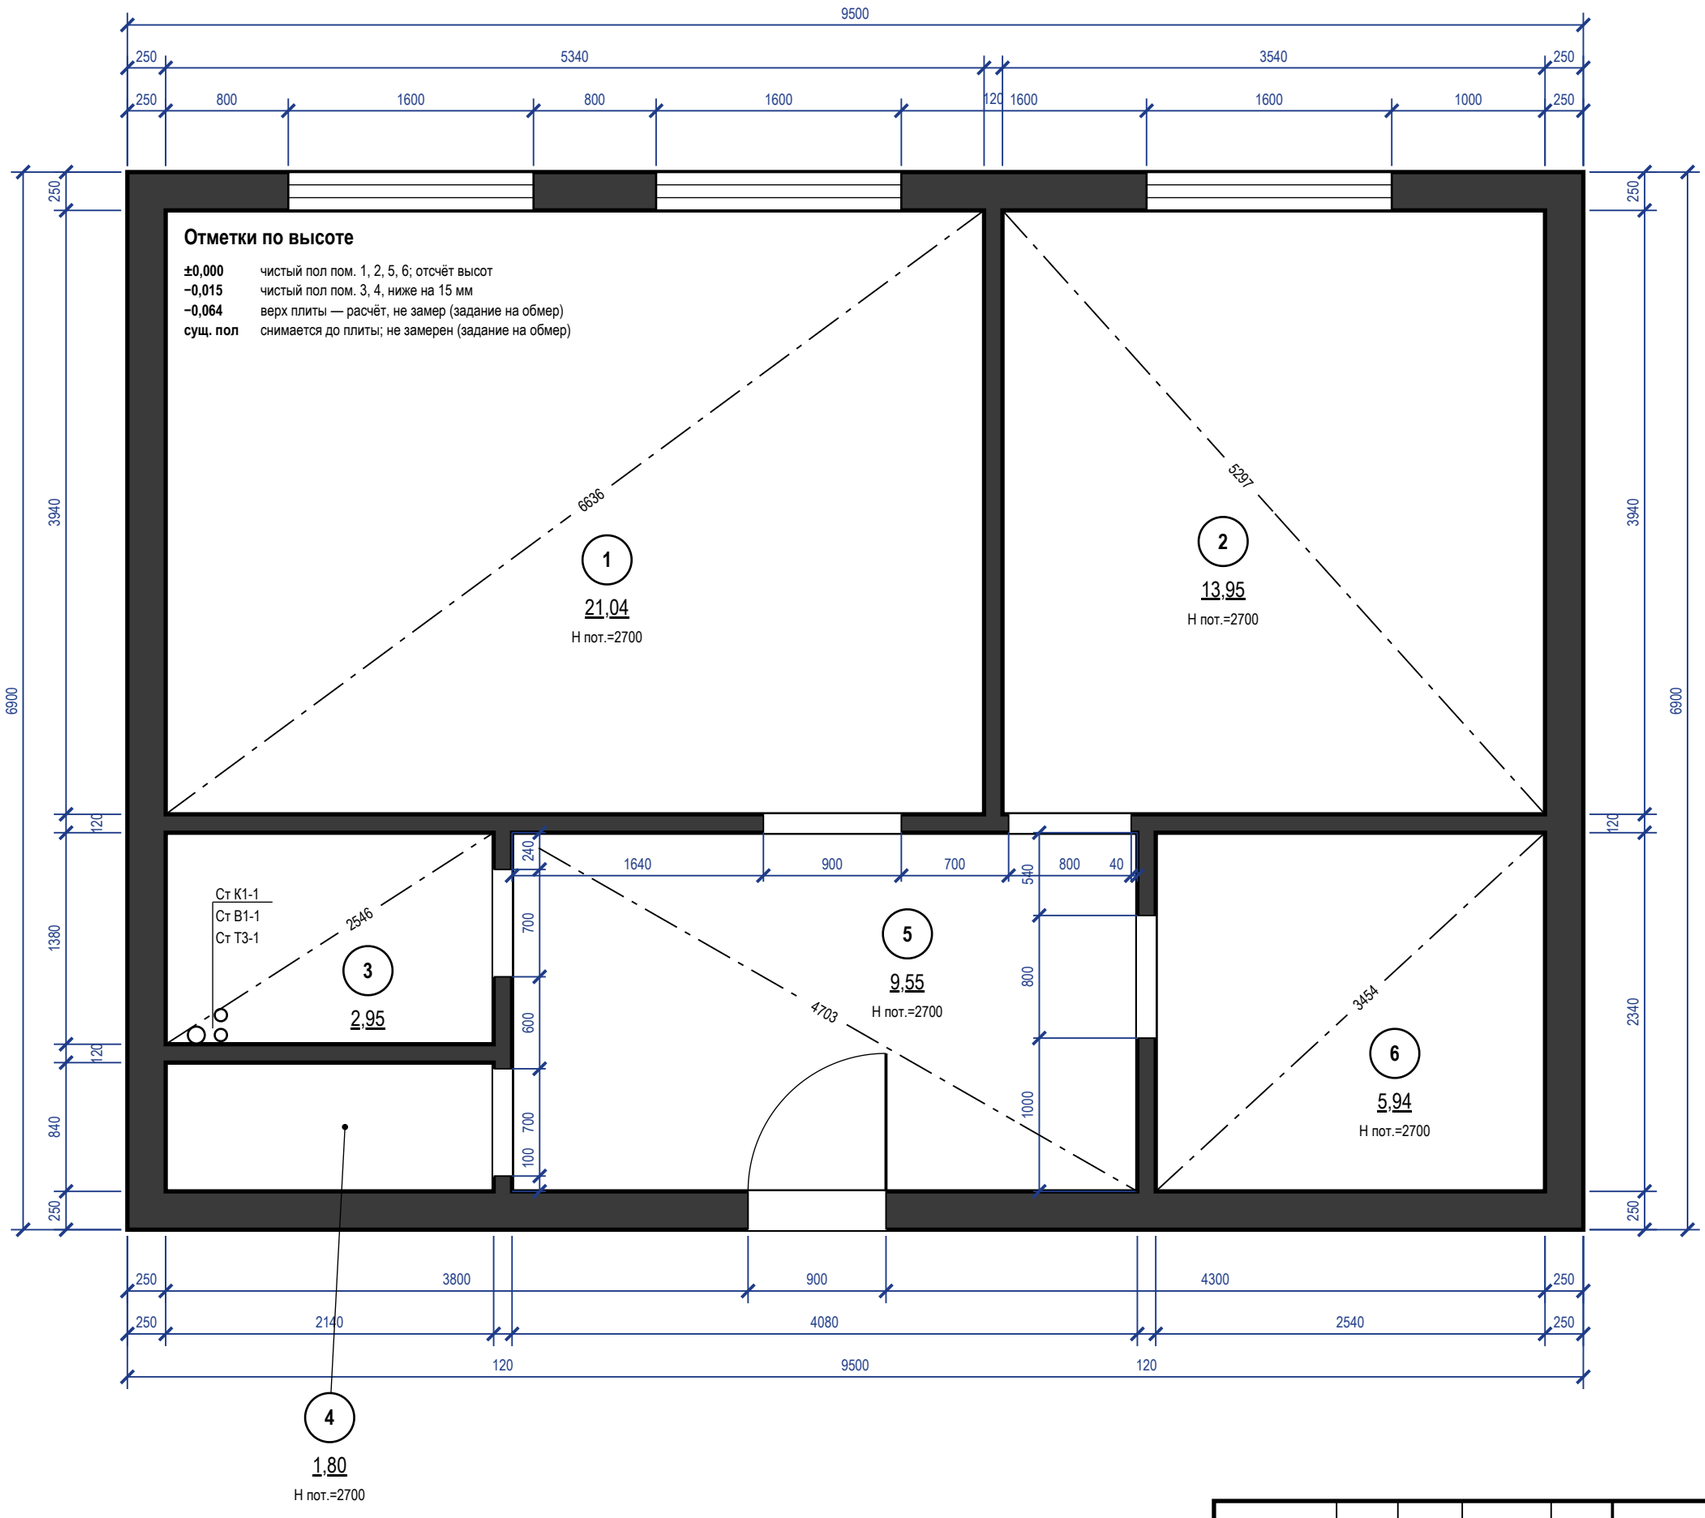

Экспликация помещений

№	Наименование	Площадь, м²
1	Кухня-гостиная	21,04
2	Спальня	13,95
3	Ванная	2,95
4	Санузел	1,80
5	Прихожая	9,55
6	Гардеробная	5,94
	Итого (общая площадь)	**55,23**

Условные обозначения

- существующие стены (сечение)
- окно (рама, остекление)
- проём существующий, без заполнения (откосы)
- стояк: К1 — канализация, В1 — ХВС, Т3 — ГВС
- диагональ помещения — контроль прямоугольности
- (1) номер помещения, площадь м²

Примечания

1. Размеры — в мм по чистым поверхностям стен до отделки (по плану заказчика); площади — в м² по тем же размерам. До начала работ выполнить контрольный обмер.
2. За отметку ±0,000 принят чистый пол, не существующий (блок отметок). Н пот. — высота от чистого пола до плиты перекрытия.
3. Толщины стен: наружные 250 мм, перегородки 120 мм; отличающиеся толщины и уступы — размерами на плане.
4. Несущие стены не определены: до технического заключения все стены считать несущими; проёмы и штробы в них не выполнять.
5. Дверные проёмы показаны без заполнения (двери — лист 15); высота дверных проёмов 2100 мм; низ окон (подоконник) 800 мм от чистого пола, высота окон 1600 мм.
6. Диагонали — контрольные размеры; расхождение более 5 мм подписать на плане как перекос.
7. Размеры проверить на месте до начала работ; расхождение контрольных промеров ≤ 2 %.


					Проект: Квартира 58 м²
	Лист	№ док.	Подпись	Дата	План планировки от заказчика
Дизайнер	Кырлан А.С.			09.10.26	

Стадия	Лист	Листов
П	3	60

Правка к этому листу

Экспликация помещений

№	Наименование	Площадь, м²
1	Кухня-гостиная	21,04
2	Спальня	13,95
3	Ванная	2,95
4	Санузел	1,80
5	Прихожая	9,55
6	Гардеробная	5,94
	Итого (общая площадь)	**55,23**

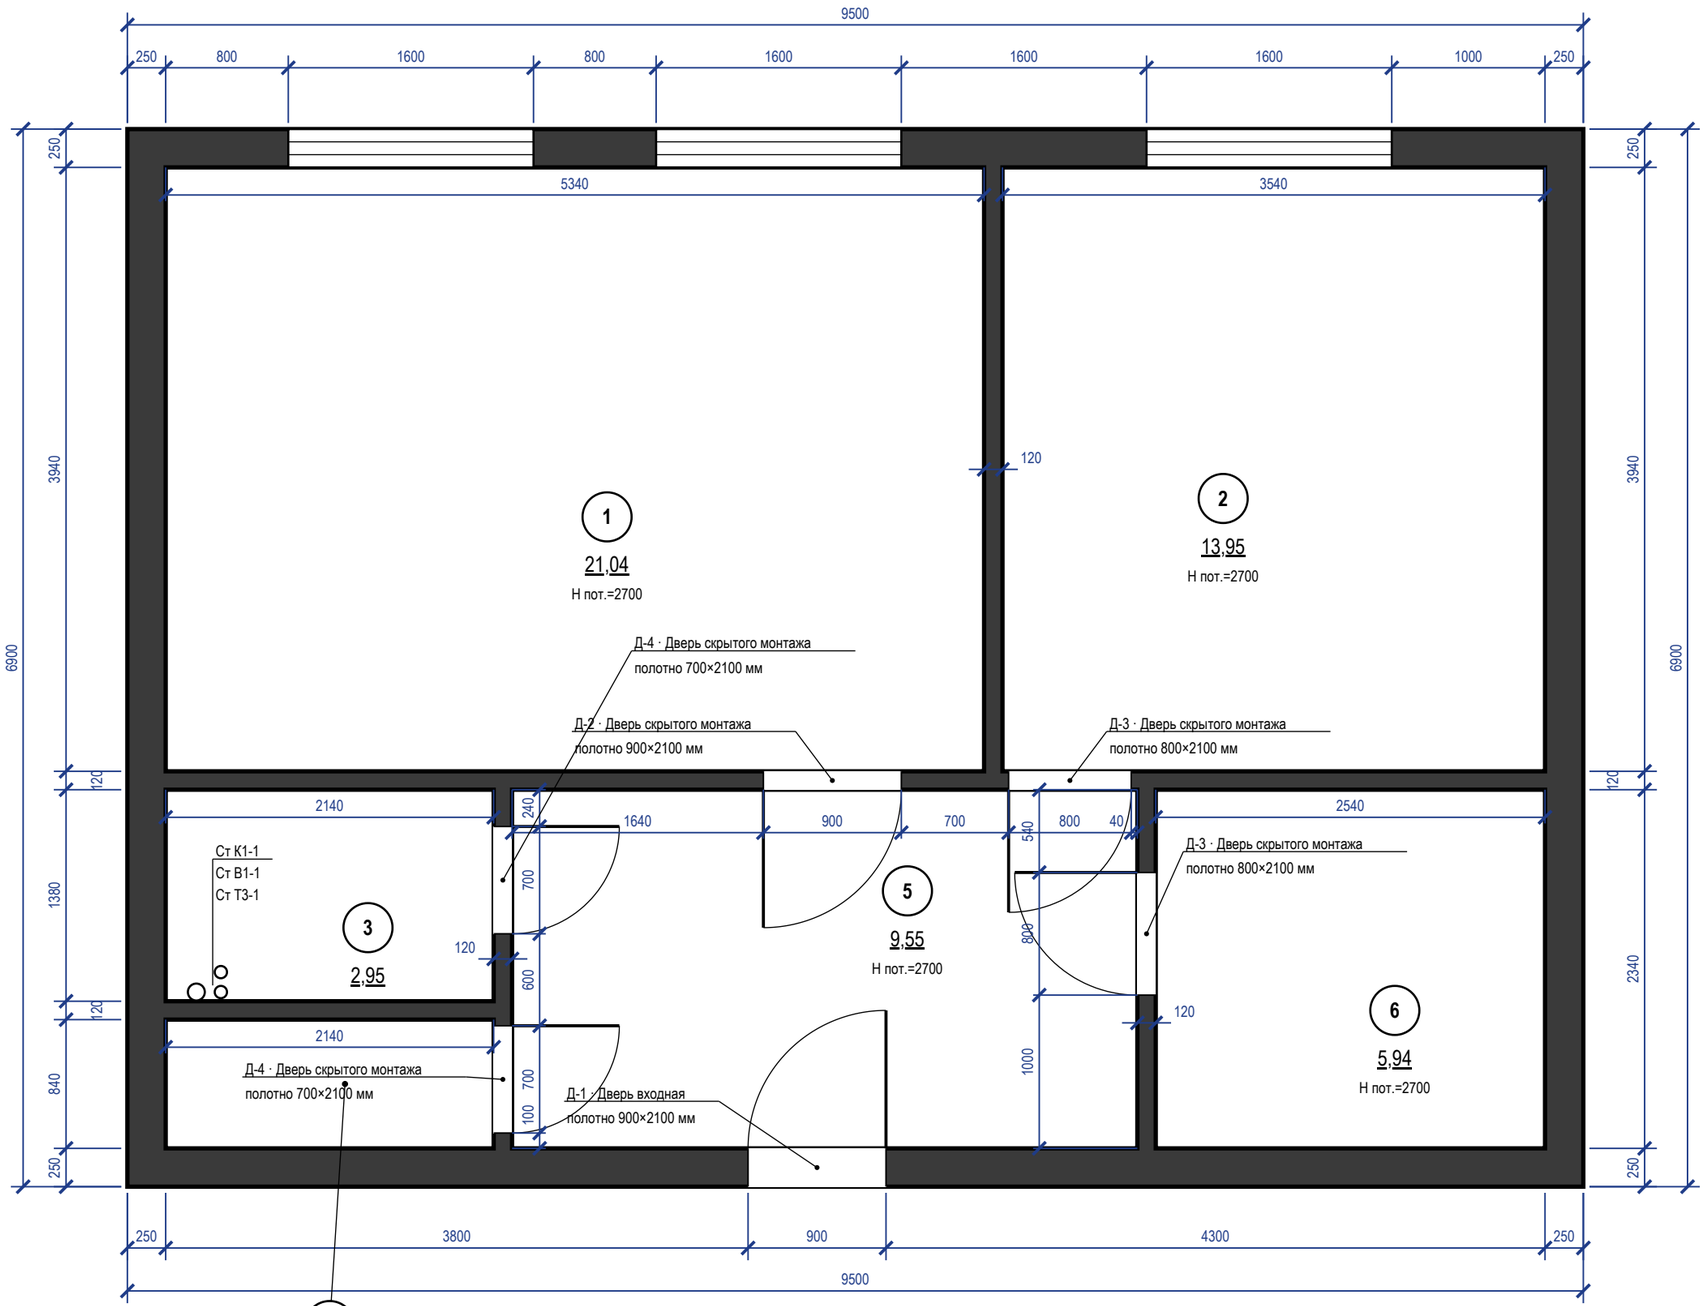

4
1,80
Н пот.=2700

Примечания

1. Размеры — в мм от чистовых поверхностей стен до отделки; размеры уточнить по месту до начала работ.
2. Новые перегородки и облицовки — синим; каркас и обшивка — по выноскам; двери и проёмы лист 15.
3. Несущие стены не изменять: проёмы, ниши и штробы в них — только по техническому заключению.


					Проект: Квартира 58 м²
	Лист	№ док.	Подпись	Дата	План монтажный
Дизайнер	Кырлан А.С.			09.10.26	

Стадия	Лист	Листов
П	4	60


выпуск 09.10.2026 № 7efd137e8f · стр. 4 из 60

Правка к этому листу

Привязка выводов и крепление модулей

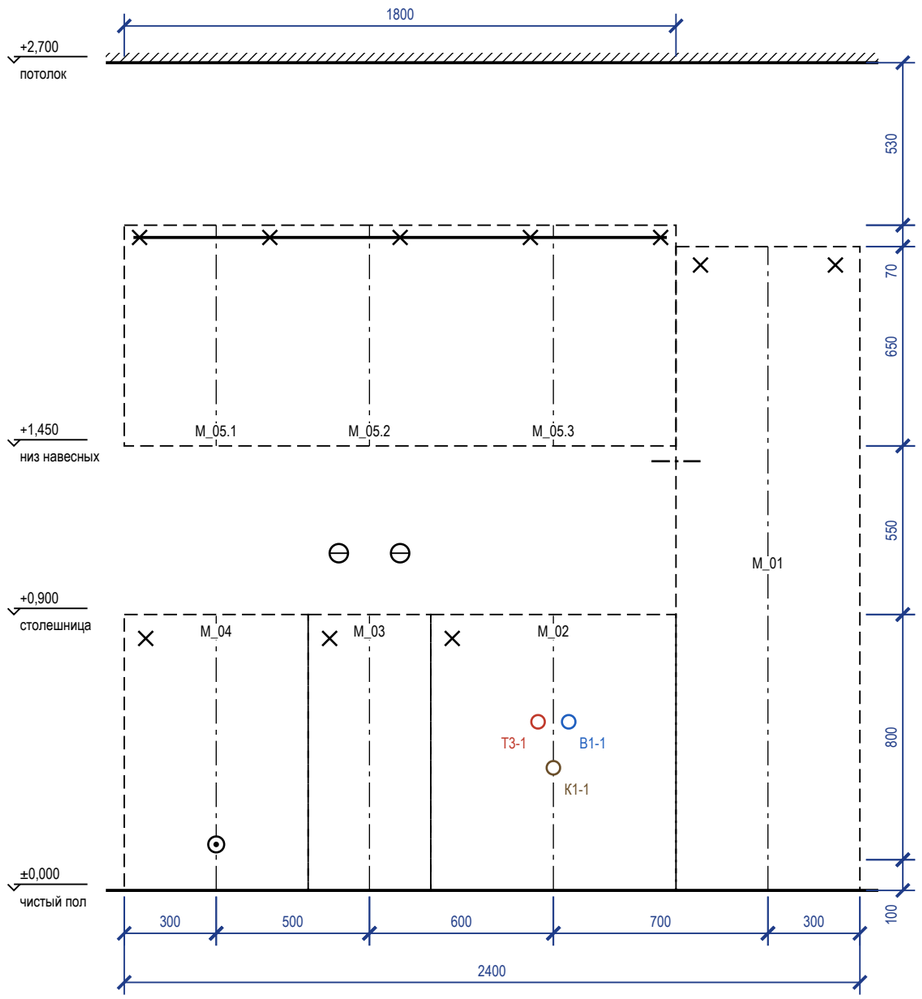

План столешницы

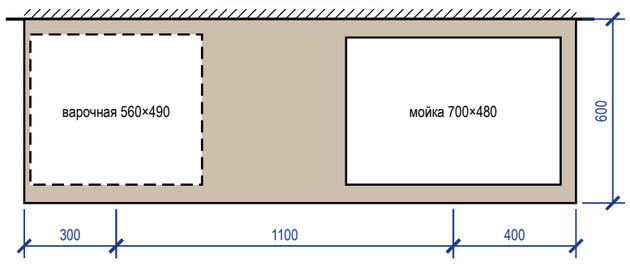

Привязка выводов к осям модулей

Код	Назначение	Модуль	От оси, мм	H, мм	Размещение
	вывод кабеля — варочная панель	M_04	0	150	в соседнем модуле, за ящиком
	розетка — рабочая зона	M_03	−100	1100	над столешницей (фартук)
	розетка ×2 — рабочая зона	M_03	+100	1100	над столешницей (фартук)
T3-1	T3 — межос. 100	M_02	−50	550	в модуле мойки
K1-1	K1 Ø50 — мойка	M_02	0	400	в модуле мойки
B1-1	B1 — межос. 100	M_02	+50	550	в модуле мойки
	светодиодная лента — подсветка столешницы	M_01	−300	1400	за пеналом

Зазоры под отделку

Поверхность	Отделка	Зазор, мм	Учесть
фартук	плитка / стеновая панель	10	от чернового основания до корпуса навесных и столешницы
стены	окраска	5	под штукатурку и шпаклёвку за пеналом
пол	инженерная доска		цоколь — после укладки пола, опоры ±20 мм

Условные обозначения

- навесной модуль (невидимый контур)
- ось модуля (от неё — привязка вывода)
- анкер / уголок крепления к стене
- розетка на стене
- вывод кабеля к технике
- B1 — вывод воды B1 / T3, канализации K1

Примечания

1. Выводы — по проекту электрики и ВК; привязка по горизонтали — от оси модуля (плюс — вправо по виду), по высоте — от чистого пола до оси вывода.
2. Пенал — уголки к стене 2 шт. сверху; нижние модули — стяжками между собой и уголком к стене; ряд выставить по уровню опорами цоколя.
3. Розетки над столешницей — не ниже 150 мм над ней и не за корпусом техники; розетка за ПММ, духовым шкафом и холодильником — только в соседнем модуле или в зоне цоколя с доступом.
4. Столешница — вырезы по шаблонам выбранных моделей мойки и варочной панели; торцы у стены — герметик, пристеночный плинтус.


					Проект: Квартира 58 м²
	Лист	№ док.	Подпись	Дата	Кухня (пом. 1). Монтажная схема
Дизайнер	Кырлан А.С.			09.10.26	

Стадия	Лист	Листов
П	5	60


выпуск 09.10.2026 № 7efd137e8f · стр. 5 из 60

Правка к этому листу

Шкаф-купе М_13 (пом. 5)

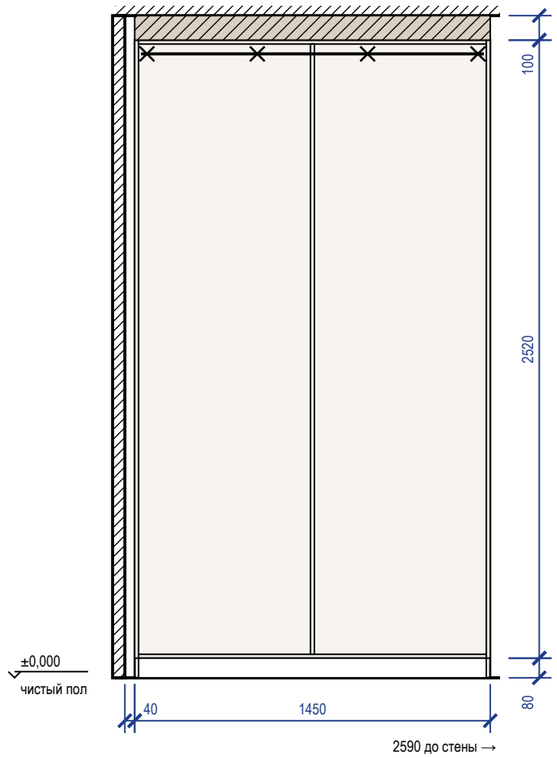

Система хранения М_14 (пом. 6)

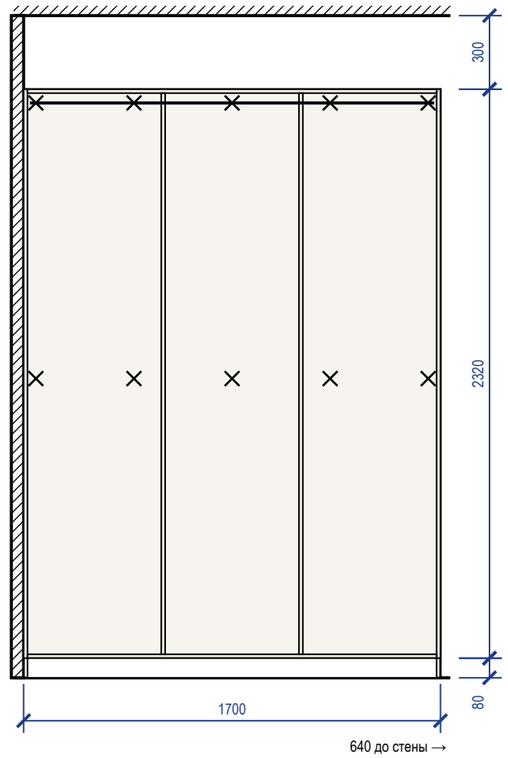

Крепление и зазоры под отделку

Марка	Помещение, стена	Основание	Отделка стены	Зазор, мм	Крепёж по планке	От опрокидывания
М_13	Прихожая (5), стена В	по основанию — см. таблицу крепежа	окраска	5	анкер 4 шт., шаг 450	уголки 2 шт.
М_14	Гардеробная (6), стена Б	по основанию — см. таблицу крепежа	окраска	5	анкер 10 шт. (2 ряда)	крепление к стене, 3 точки

Крепёж по основанию стены

Основание стены	Крепёж
бетон, ж/б	анкер-шуруп 7,5×72 или дюбель 8×60 с шурупом 5×70
кирпич полнотелый	дюбель 8×80 с шурупом 5×90
газобетон, пазогребень	дюбель для газобетона 10×100 или химический анкер
гипсокартон	закладная до обшивки (брус 40×80 или фанера 18 мм), саморез в закладную

Условные обозначения

- × — анкер / уголок крепления к стене
- корпус и полки ЛДСП (вид на стену)
- компенсатор — короб до потолка

Примечания

1. Установочные размеры — от чистого пола и чистых стен; перед установкой контрольный замер после отделки.
2. Порядок: корпус выставить по уровню опорами цоколя → закрепить к стене по задней планке → навесить двери и фасады, отрегулировать зазоры → подогнать и закрепить компенсатор.
3. Анкеры — с шагом не более 500 мм, не ближе 50 мм от края планки; на ГКЛ только в закладную, установленную до обшивки.
4. Скрытые коммуникации под анкеры проверить детектором; трассы электрики по плану розеток.

	Лист	№ док.	Подпись	Дата
Дизайнер	Кырлан А.С.			09.10.26


Проект: Квартира 58 м²

Шкафы. Монтажная схема

Стадия	Лист	Листов
П	6	60

выпуск 09.10.2026 № 7efd137e8f · стр. 6 из 60

Правка к этому листу

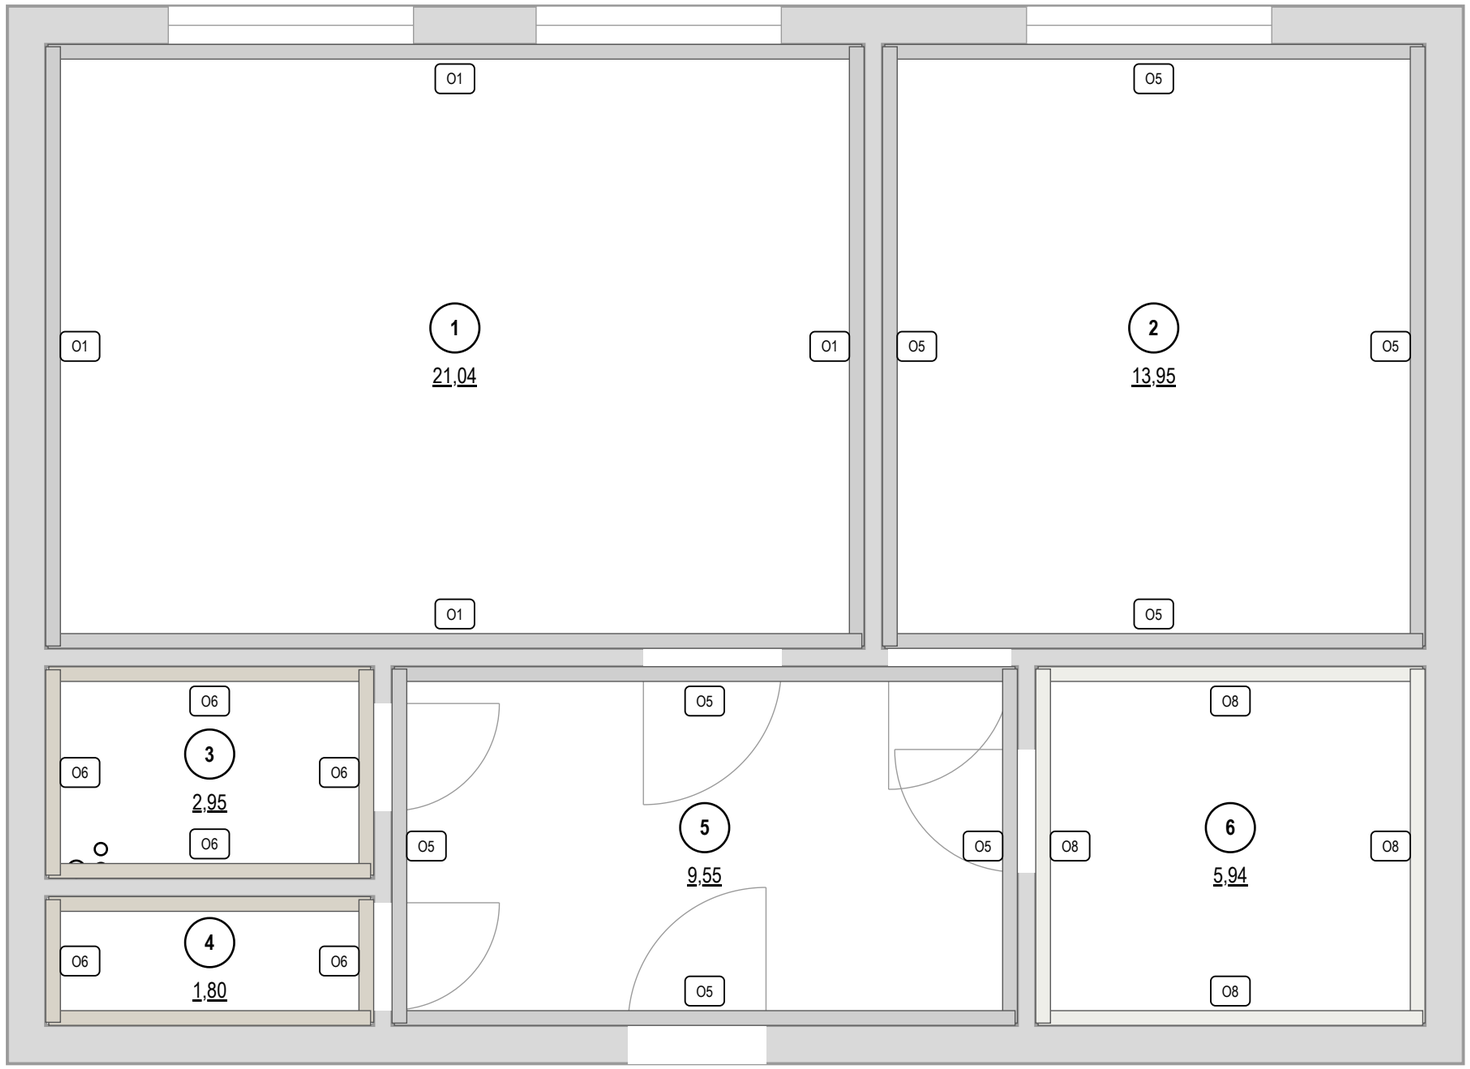

Покрытия стен

Марка	Покрытие	Помещение: S, м²	Итого, м²
О1	окраска Tikkurila · S 1002-Y50R	1: 42,8	42,8
О5	окраска Tikkurila · S 1502-Y50R	2: 35,8; 5: 24,3	60,1
О6	облицовка плиткой Italon · 610015000370 «Charme Extra» 600×1200 мм	3: 17,2; 4: 14,3	31,5
О8	окраска Tikkurila · V503 «Winter»	6: 24,3	24,3

Площади — нетто, по развёрткам (за вычетом проёмов и фартука); высоты помещений — от чистого пола.

					Проект: Квартира 58 м²
	Лист	№ док.	Подпись	Дата	
Дизайнер	Кырлан А.С.			09.10.26	Карта покрытий стен
					Стадия: П; Лист: 7; Листов: 60

выпуск 09.10.2026 № 7efd137e8f · стр. 7 из 60

Правка к этому листу

Колерная карта по помещениям

Помещение	Поверхность	Образец	Поз.	Система и код цвета	Производитель, линейка / материал, артикул	Блеск	Класс EN 13300	LRV	Площадь
1. Кухня-гостиная 21,04 м²	стены		**К1**	NCS S 1002-Y50R	Tikkurila	полуматов.	1	82	43,1 м²
	потолок		**К2**	NCS S 0300-N	Tikkurila	глубокомат.	1	92	21,0 м²
	пол		**КМ1**	по образцу	Quick-Step · Impressive				21,0 м²
	плинтус		**К3**	NCS S 0300-N	Orac Decor · Luxxus	полуматов.		92	17,7 м
2. Спальня 13,95 м²	стены		**К4**	NCS S 1502-Y50R	Tikkurila	глубокомат.	2	72	36,2 м²
	потолок		**К5**	NCS S 0300-N	Tikkurila	глубокомат.	2	92	13,9 м²
	пол		**КМ1**	по образцу	Quick-Step · Impressive				13,9 м²
	плинтус		**К3**	NCS S 0300-N	Orac Decor · Luxxus	полуматов.		92	14,2 м
3. Ванная 2,95 м²	стены		**К6**	Italon 610015000370	Italon · Charme Extra				17,6 м²
	потолок		**К2**	NCS S 0300-N	Tikkurila	глубокомат.	1	92	3,0 м²
	пол		**К7**	Kerama Marazzi SG651622R	Kerama Marazzi · Две Венеции / Риальто				3,0 м²
4. Санузел 1,8 м²	стены		**К6**	Italon 610015000370	Italon · Charme Extra				14,7 м²
	потолок		**К2**	NCS S 0300-N	Tikkurila	глубокомат.	1	92	1,8 м²
	пол		**К7**	Kerama Marazzi SG651622R	Kerama Marazzi · Две Венеции / Риальто				1,8 м²
5. Прихожая 9,55 м²	стены		**К8**	NCS S 1502-Y50R	Tikkurila	полуматов.	1	72	24,6 м²
	потолок		**К2**	NCS S 0300-N	Tikkurila	глубокомат.	1	92	9,6 м²
	пол		**К7**	Kerama Marazzi SG651622R	Kerama Marazzi · Две Венеции / Риальто				9,6 м²
	плинтус		**К3**	NCS S 0300-N	Orac Decor · Luxxus	полуматов.		92	8,0 м
6. Гардеробная 5,94 м²	стены		**К9**	Tikkurila V503	Tikkurila · Harmony	матовая	1	86	24,7 м²
	потолок		**К10**	Tikkurila V503	Tikkurila · Anti-Reflex 2	глубокомат.	2	86	5,9 м²
	пол		**КМ1**	по образцу	Quick-Step · Impressive				5,9 м²
	плинтус		**К11**	Tikkurila V503	Orac Decor · Luxxus			86	9,0 м

Перечень выкрасов на согласование

№	Код	Бренд / веер	Пом. / стена	Подложка	Формат	Статус
1	S 1002-Y50R	NCS Tikkurila	1	ГКЛ, загрунтованный под эту краску	600×1000	к выполнению
2	S 0300-N	NCS Tikkurila	1, 2, 3, 4, 5	ГКЛ, загрунтованный под эту краску; МДФ, загрунтованный под эмаль	600×1000; 300×600	к выполнению
3	S 1502-Y50R	NCS Tikkurila	2, 5	ГКЛ, загрунтованный под эту краску	600×1000	к выполнению
4	V503	Tikkurila	6	ГКЛ, загрунтованный под эту краску; МДФ, загрунтованный под эмаль	600×1000; 300×600	к выполнению

Примечания

1. Цвет утверждается только по выкрасу на объекте: формат от А3 до 1000×1000 мм на загрунтованном ГКЛ, в 2 слоя (как на стене), не на белой шпаклёвке; смотреть днём и при свете проекта своего помещения, рядом с образцами пола и фасадов. Подпись на обороте: код, бренд и веер, дата.
2. Колеровка машинная в колеровочном центре бренда; каждый код — за один проход, одной партией на весь объём. Колеровщику передаётся только система и код утверждённого веера; плашки и HEX на листе — ориентир, печать не является эталоном цвета.
3. Класс мокрого истирания — EN 13300 (ISO 11998); блеск — по ГОСТ 31975 (ISO 2813), геометрия 60°. LRV — пересчёт координаты L каталога производителя (Y = ((L*+16)/116)³); «≈» — расчёт по HEX, справочно.
4. Площади поверхностей — тем же способом и с теми же цифрами, что в ведомости отделки (способ счёта — в общих указаниях); объём краски к заказу, фасовка и материалы КМ — в спецификации отделочных материалов.
5. Перечень выкрасов составлен по кодам колерной карты; к основному тону стен добавить на выкрас 2 соседних тона того же веера (светлее и темнее), статус отмечать в графе «Статус» при согласовании.

Схема квартиры: цвет стен и акценты (б/м)

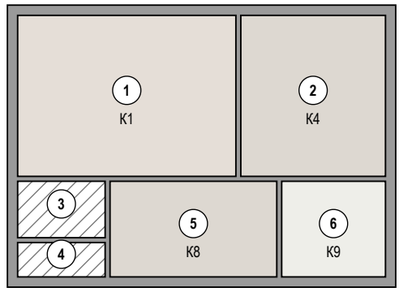


Схема палитры проекта


Стиль: Скандинавский · схема: нейтральная

основной	второстепенный	второстепенный	акцентный
NCS S 0500-N	**NCS S 1500-N**	**NCS S 2002-Y**	**NCS S 4010-R90B**
нейтральный белый	светлый нейтральный серый	серый камень, тёплый	пыльный синий
LRV 85	LRV 64	LRV 55	LRV 27
в отделке не применён	в отделке не применён	в отделке не применён	в отделке не применён

План 60/30/10



Окраска, факт — по площади стен, акцентов, потолков

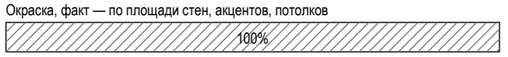

окрашено всего 216,1 м²; второстепенный тон несут мебель и текстиль

Условные обозначения

- **К1** NCS S 1002-Y50R · Tikkurila · полуматов. · кл. 1
- **К2** NCS S 0300-N · Tikkurila · глубокомат. · кл. 1
- **К3** NCS S 0300-N · Orac Decor Luxxus · полуматов.
- **К4** NCS S 1502-Y50R · Tikkurila · глубокомат. · кл. 2
- **К5** NCS S 0300-N · Tikkurila · глубокомат. · кл. 2
- **К6** Italon 610015000370 · Charme Extra · Charme Extra
- **К7** Kerama Marazzi SG651622R · Две Венеции / Риальто · Две Венеции / Риальто
- **К8** NCS S 1502-Y50R · Tikkurila · полуматов. · кл. 1
- **К9** Tikkurila V503 · Winter · Harmony · матовая · кл. 1
- **К10** Tikkurila V503 · Winter · Anti-Reflex 2 · глубокомат. · кл. 2
- **К11** Tikkurila V503 · Winter · Luxxus
- **КМ1** инженерная доска · IM1861

дерево (доска, паркет, ламинат) — рисунок досок


HEX не задан — цвет только по коду и вееру

К — позиция окраски (код + продукт + блеск), КМ — позиция материала, тон КМ — по описанию артикула, эталон — образец материала; ≈ LRV — расчёт по HEX, справочно

					Проект: Квартира 58 м²
	Лист	№ док.	Подпись	Дата	
Дизайнер	Кырлан А.С.			09.10.26	Колерная карта

Стадия	Лист	Листов
П	8	60

выпуск 09.10.2026 № 7efd137e8f · стр. 8 из 60

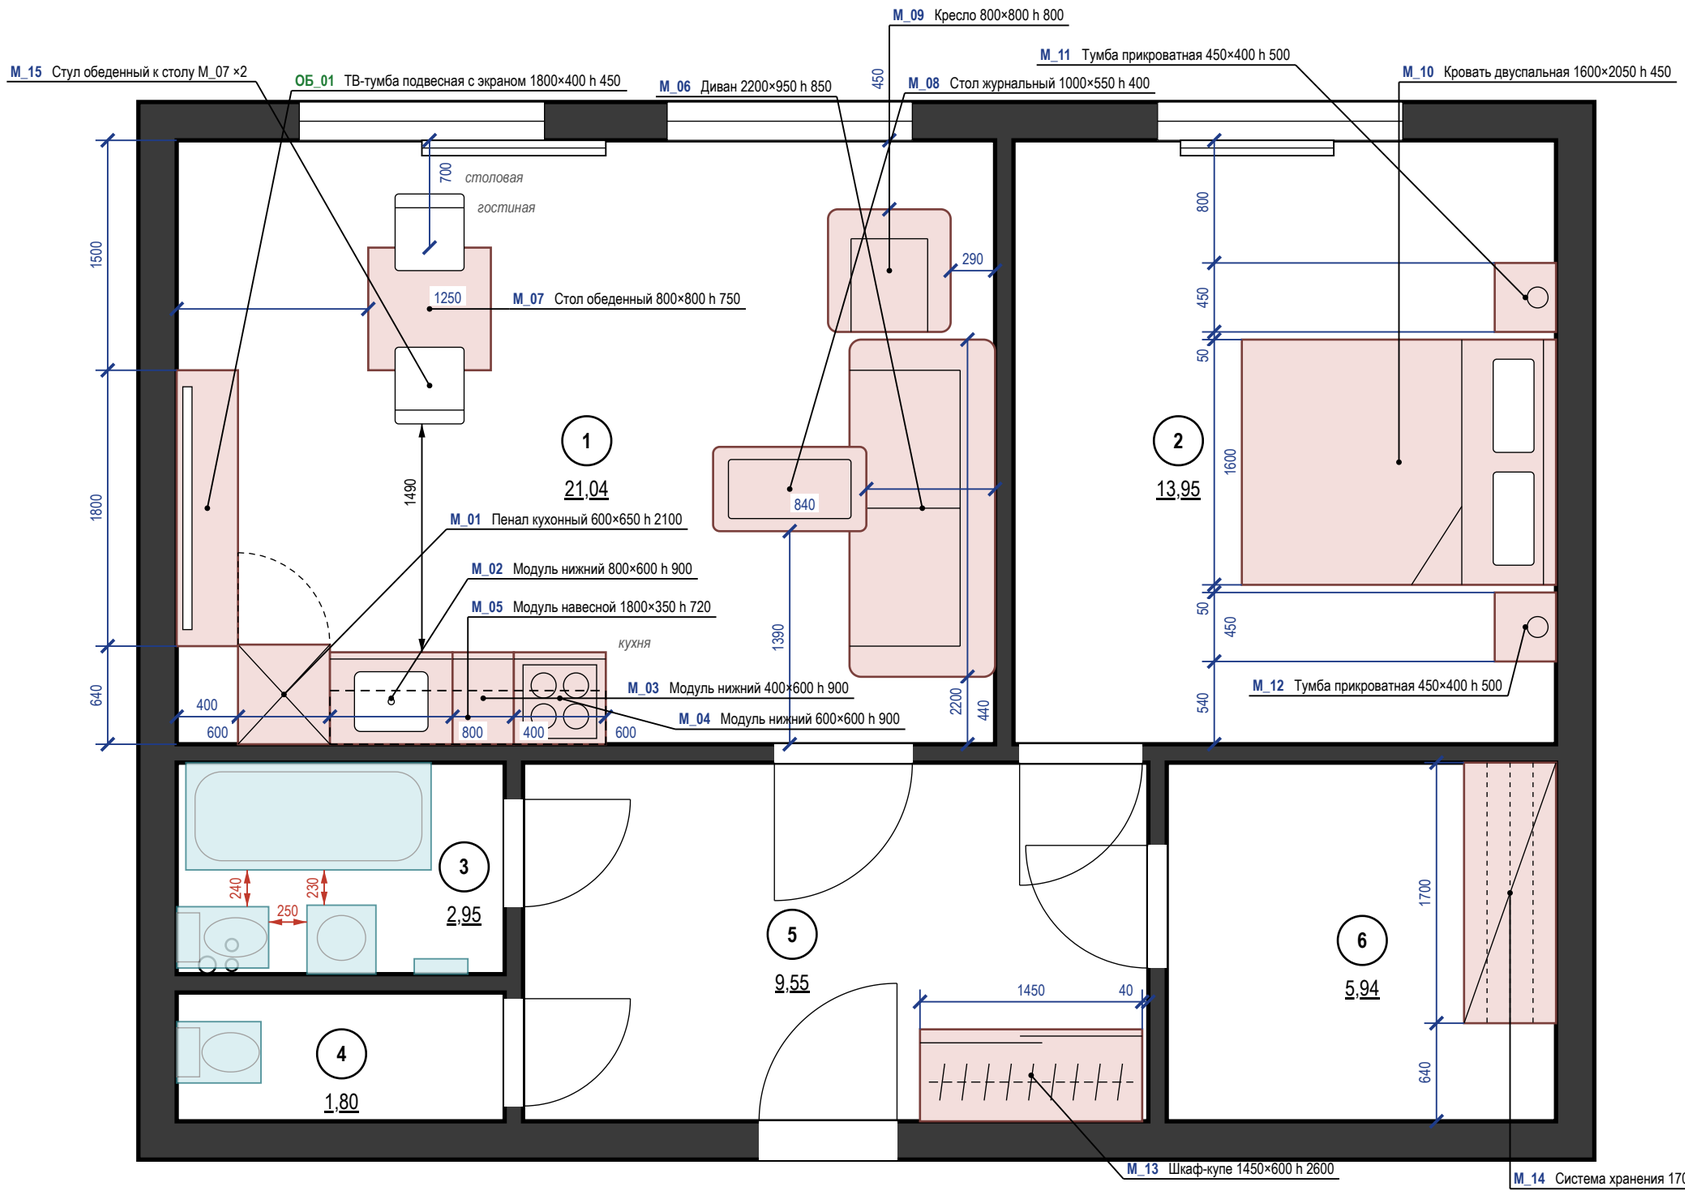

Экспликация помещений

лист обмерного плана · на плане — номера в марках

Ведомость мебели и оборудования

Марка	Наименование	Ш×Г×В, мм	Пом.	Кол.
М_01	Пенал кухонный	600×650×2100	1	1
М_02	Модуль нижний	800×600×900	1	1
М_03	Модуль нижний	400×600×900	1	1
М_04	Модуль нижний	600×600×900	1	1
М_05	Модуль навесной	1800×350×720	1	1
М_06	Диван	2200×950×850	1	1
М_07	Стол обеденный	800×800×750	1	1
ОБ_01	ТВ-тумба подвесная с экраном	1800×400×450	1	1
М_08	Стол журнальный	1000×550×400	1	1
М_09	Кресло	800×800×800	1	1
М_10	Кровать двуспальная	1600×2050×450	2	1
М_11	Тумба прикроватная	450×400×500	2	1
М_12	Тумба прикроватная	450×400×500	2	1
М_13	Шкаф-купе	1450×600×2600	5	1
М_14	Система хранения	1700×600×2400	6	1
М_15	Стул обеденный к столу М_07	450×500×820	1	2

Ш — вдоль стены (изголовья), Г — от стены (длина кровати)

Материалы, модели, допуск замены — лист 10

Примечания

1. Размеры — в мм от чистовых поверхностей стен; размеры мебели уточнить после отделочных работ; общие указания — лист 2.
2. Стулья обеденной группы (М_15 — 2 шт.) показаны в рабочем положении, задвинутыми под столешницу на 150 мм.

					Проект: Квартира 58 м²
	Лист	№ док.	Подпись	Дата	План размещения мебели и оборудования
Дизайнер	Кырлан А.С.			09.10.26	

Стадия	Лист	Листов
П	9	60

выпуск 09.10.2026 № 7efd137e8f · стр. 9 из 60

Правка к этому листу

Поз.	Наименование и техническая характеристика	Тип, марка, обозначение документа, опросного листа	Код продукции	Поставщик	Ед. измерения	Кол.	Масса 1 ед., кг	Примечание
	Мебель встроенная и корпусная (изготовление по чертежам мебельщика)							
М_01	Пенал кухонный, холодильник; корпус ЛДСП 16 мм, фасады МДФ эмаль; Ш×Г×В 600×650×2100 мм			изготовление на заказ	шт.	1		пом. 1
М_02	Модуль нижний, мойка; корпус ЛДСП 16 мм, фасады МДФ эмаль; Ш×Г×В 800×600×900 мм			изготовление на заказ	шт.	1		пом. 1
М_03	Модуль нижний; корпус ЛДСП 16 мм, фасады МДФ эмаль; Ш×Г×В 400×600×900 мм			изготовление на заказ	шт.	1		пом. 1
М_04	Модуль нижний, варочная; корпус ЛДСП 16 мм, фасады МДФ эмаль; Ш×Г×В 600×600×900 мм			изготовление на заказ	шт.	1		пом. 1
М_05	Модуль навесной; корпус ЛДСП 16 мм, фасады МДФ эмаль; Ш×Г×В 1800×350×720 мм			изготовление на заказ	шт.	1		пом. 1
М_13	Шкаф-купе; корпус ЛДСП, фасады — матовая эмаль в цвет стен (NCS S 1502-Y50R); Ш×Г×В 1450×600×2600 мм			изготовление на заказ	шт.	1		пом. 5
М_14	Система хранения: штанги, полки, ящики; каркас и полки — ЛДСП, декор «дуб натуральный»; Ш×Г×В 1700×600×2400 мм			изготовление на заказ	шт.	1		пом. 6; крепление к стене
	Мебель покупная							
М_06	Диван; обивка — ткань, цвет NCS S 1500-N; Ш×Г×В 2200×950×850 мм			аналог по характеристикам	шт.	1		пом. 1; замена ≤ габарита
М_07	Стол обеденный; шпон, дуб натуральный, матовое масло; Ш×Г×В 800×800×750 мм			аналог по характеристикам	шт.	1		пом. 1; замена ≤ габарита
М_08	Стол журнальный; шпон, дуб натуральный, матовое масло; Ш×Г×В 1000×550×400 мм			аналог по характеристикам	шт.	1		пом. 1; замена ≤ габарита
М_09	Кресло; обивка — ткань, цвет NCS S 1500-N; Ш×Г×В 800×800×800 мм			аналог по характеристикам	шт.	1		пом. 1; замена ≤ габарита
М_15	Стул обеденный к столу М_07; обивка — ткань, цвет NCS S 1500-N; каркас — дуб натуральный; Ш×Г×В 450×500×820 мм			аналог по характеристикам	шт.	2		пом. 1; замена ≤ габарита
ОБ_01	ТВ-тумба подвесная с экраном; шпон, дуб натуральный, матовое масло; Ш×Г×В 1800×400×450 мм			аналог по характеристикам	шт.	1		пом. 1; замена ≤ габарита
М_10	Кровать двуспальная; мягкое изголовье, обивка — ткань, цвет NCS S 1500-N; Ш×Г×В 1600×2050×450 мм			аналог по характеристикам	шт.	1		пом. 2; замена ≤ габарита
М_11, М_12	Тумба прикроватная; шпон, дуб натуральный, матовое масло; Ш×Г×В 450×400×500 мм			аналог по характеристикам	шт.	2		пом. 2; замена ≤ габарита
	Техника встраиваемая и бытовая, светильники под розетки							
	Холодильник, в модуле М_01			аналог по характеристикам	шт.	1		пом. 1; по схеме изготовителя
	Варочная панель встраиваемая, электрическая, в модуле М_04			аналог по характеристикам	шт.	1		пом. 1; по схеме изготовителя
	Торшер, у поз. М_07; абажур — ткань или опаловое стекло; лампа 3000 K			аналог по характеристикам	шт.	1		пом. 1; розетка — по плану розеток (ЭОМ)

Примечания

1. Позиции мебели совпадают с марками на плане расстановки; размеры Ш×Г×В — Ш вдоль стены, Г от стены.
2. Встроенная и корпусная мебель изготавливается по чертежам мебельщика после контрольного обмера; графы «Тип, марка» и «Код продукции» для неё не заполняются (ГОСТ 21.110-2013).
3. Покупные изделия — аналог по характеристикам: заменять только на изделия не больше указанного габарита и того же материала и цвета.
4. Материал и цвет, не указанные в данных изделия, приняты по концепции: тон дерева — по полу, обивка — по вторичному цвету палитры; образцы согласовать до заказа.
5. Масса 1 ед. для изделий до 25 кг не указывается. Техника — по монтажным схемам изготовителя; выводы — по листам ЭОМ и ВК.

					Проект: Квартира 58 м²
	Лист	№ док.	Подпись	Дата	Спецификация мебели и оборудования
Дизайнер	Кырлан А.С.			09.10.26	Стадия: П; Лист: 10; Листов: 60

Правка к этому листу

Ведомость изделий

Марка	Наименование	Пом.	Ш×Г×В, мм	Корпус	Фасад	Кромка, мм скр./вид.	Кол.
M_13	Шкаф-купе	5	1450×600×2600	ЛДСП 16	рифлёные панели МДФ в алюминиевом профиле	0,4 / 1	1
M_14	Система хранения	6	1700×600×2400	ЛДСП 16	без фасадов; ящики — МДФ 18, эмаль матовая	0,4 / 2	1
M_04	Модуль нижний: ящики, варочная	1	600×600×900	ЛДСП 16	МДФ эмаль	0,4 / 1	1
M_05	Модуль навесной: полки, сушка	1	1800×350×720	ЛДСП 16	МДФ эмаль	0,4 / 1	1
M_03	Модуль нижний: ящики	1	400×600×900	ЛДСП 16	МДФ эмаль	0,4 / 1	1
M_02	Модуль нижний: мойка	1	800×600×900	ЛДСП 16	МДФ эмаль	0,4 / 1	1
M_01	Пенал: холодильник	1	600×650×2100	ЛДСП 16	МДФ эмаль	0,4 / 1	1

Ведомость встраиваемой техники

Поз.	Прибор	Ниша, вырез, мм	Вентиляция	Питание	Схема
M_04	Варочная панель индукционная, 60 см	вырез в столешнице 560 × 490		вывод кабеля под модулем	по модели
M_02	Мойка врезная / подстольная с сифоном	вырез по шаблону, ориентир 700 × 480		смеситель — выводы ВК	по модели
M_01	Холодильник отдельностоящий	проём 600, зазор сверху ≥ 50	по паспорту модели	розетка рядом, не за корпусом	по модели
M_04	Вытяжка настенная, 60 см	низ ≥ 650 над панелью	воздуховод к вентканалу, короб до потолка	вывод кабеля в коробе	по модели

Ведомость фурнитуры

№	Фурнитура	Тип, размер	Изделия	Кол.
1	Система дверей купе: профиль, направляющие, ролики	на 2 двери	M_13	1
2	Ручка-профиль вертикальная	в цвет профиля	M_13	2
3	Полкодержатель с фиксацией	ø5 мм	M_13, M_14, M_05	64
4	Штанга овальная 30×15, L = 701	+ 2 держателя	M_13	1
5	Полка для обуви выдвижная наклонная	ширина 701	M_13	3
6	Опора регулируемая с цоколем на клипсах	ход 20 мм	M_13, M_14	14
7	Анкер по основанию стены	по таблице крепежа	M_13, M_14, M_05	19
8	Уголок крепления к стене от опрокидывания	стальной	M_13, M_14, M_01	6
9	Штанга овальная 30×15, L = 545	+ 2 держателя	M_14	3
10	Направляющие полного выдвижения с доводчиком NL 500	пара	M_04, M_03	6
11	Ручка-профиль	латунь матовая	M_04, M_05, M_03, M_02	13
12	Опора кухонная регулируемая 100–120 мм	+ клипса цоколя	M_04, M_03, M_02, M_01	18
13	Петля накладная 110° с доводчиком	чашка 35 мм	M_05, M_02	14
14	Сушка для посуды в шкаф	ширина 800	M_05	1
15	Навес регулируемый для навесного шкафа	пара на секцию	M_05	3
16	Шина монтажная	L = 1740	M_05	1


Примечания

1. Модели техники выбирает заказчик до изготовления мебели; ниши, вырезы и вентиляция — по монтажной схеме выбранной модели (условие гарантии), её номер вносится в ведомость.
2. Количество фурнитуры — по чертежам изделий; запас крепежа 5 %. Аналоги — по характеристикам (доводчик, нагрузка, ход).
3. Цвет корпусов, фасадов и профилей — по колерной карте проекта.

					Проект: Квартира 58 м²			
	Лист	№ док.	Подпись	Дата	Ведомости изделий, техники и фурнитуры	Стадия	Лист	Листов
Дизайнер	Кырлан А.С.			09.10.26		П	11	60

Правка к этому листу


Фрагмент 1. Кухня-гостиная (пом. 1)

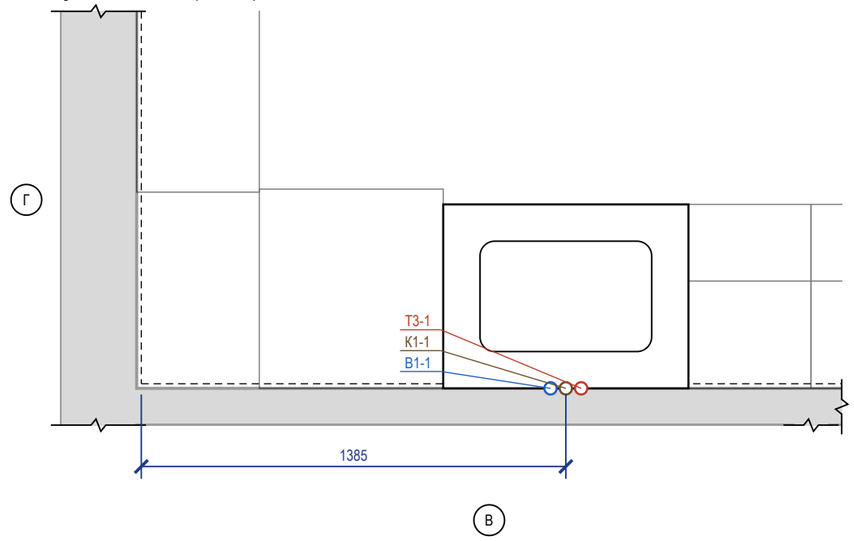


Ведомость привязок выводов

Код	Прибор	Ø	H, мм	Привязка от чист. стен, мм	Прим.
В1-1	С_01 мойка кухонная	½"	550	ст. В: 1335 от Г	межос. 100
Т3-1	С_01 мойка кухонная	½"	550	ст. В: 1435 от Г	межос. 100
К1-1	С_01 мойка кухонная	Ø50	400	ст. В: 1385 от Г	
В1-2	С_02 ванна	½"	800	ст. А: 915 от Г	межос. 150
Т3-2	С_02 ванна	½"	800	ст. А: 765 от Г	межос. 150
К1-2	С_02 ванна	Ø50	50	ст. А: 240 от Г	
В1-3	С_03 унитаз подвесной	½"	1000	ст. Г: 370 от В	в раме инсталляции
К1-3	С_03 унитаз подвесной	Ø110	220	ст. Г: 220 от В	
В1-4	С_04 умывальник	½"	550	ст. В: 1005 от Г	межос. 100
Т3-3	С_04 умывальник	½"	550	ст. В: 995 от Б	межос. 100
К1-4	С_04 умывальник	Ø50	500	ст. В: 1045 от Б	
В1-5	С_06 унитаз подвесной	½"	150	ст. Г: 220 от А	в раме инсталляции
К1-5	С_06 унитаз подвесной	Ø110	230	ст. Г: 370 от А	

Фрагмент 2. Ванная (пом. 3)

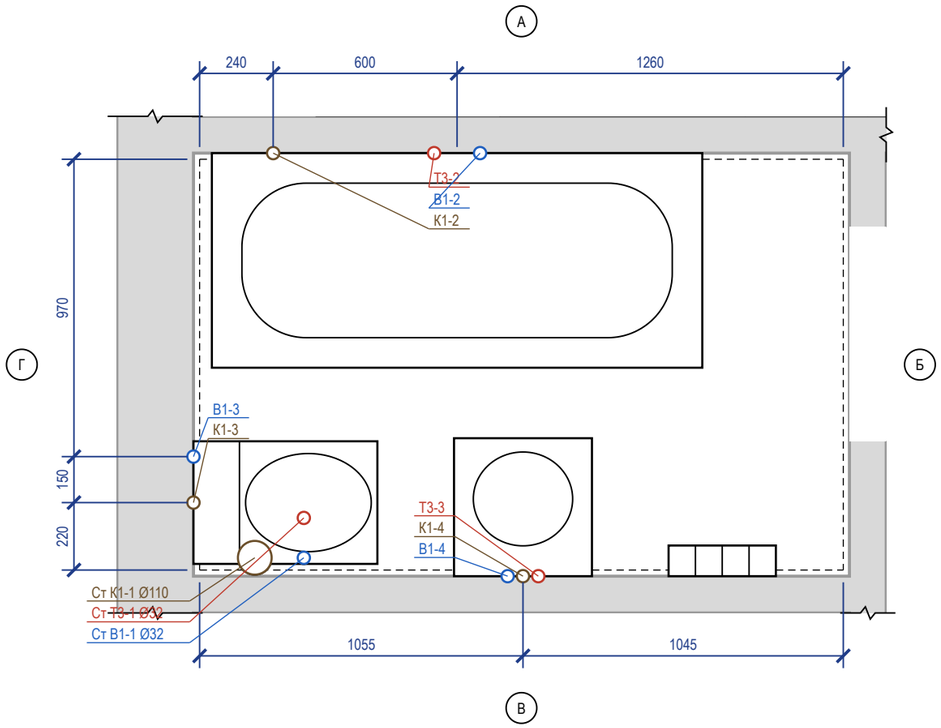

Фрагмент 3. Санузел (пом. 4)

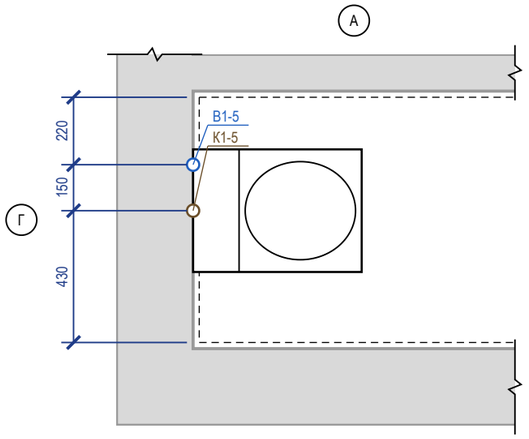

Условные обозначения

- вывод В1 (код — в ведомости привязок)
- вывод Т3 (код — в ведомости привязок)
- вывод К1 (код — в ведомости привязок)
- сантехприбор по расстановке (габарит модели)
- чистовая поверхность стены (от неё привязки)
- стояк «Ст К1-N / Ст В1-N» (ГОСТ 21.601), Ø мм
- линия обрыва (граница фрагмента)
- А — обозначение стены А–Г (как на развёртках)

Примечания


1. Привязки выводов даны от чистовых поверхностей стен (облицовка на сторону: кухня-гостиная — 15 мм (по данным); ванная — 20 мм (по данным); санузел — 20 мм (по данным)); эти же грани — на развёртках и в раскладке плитки. Высоты — от чистого пола помещения.
2. До черновой разводки сверить по паспорту выбранного прибора (смеситель, инсталляция, сифон).
3. Горячая вода (Т3) — слева от холодной (В1), если смотреть на прибор. Допуск установки выводов: ±5 мм в группе, ±20 мм у отдельно стоящих.
4. Расчёт систем водоснабжения и канализации и подбор оборудования выполняет проектная организация; лист задаёт места и высоты выводов.
5. Стояки в коробах/шахтах не замоноличивать; стояк К1 в коробе — звукоизоляция стояка в коробе без жёсткого контакта с трубой; к арматуре и ревизиям — люк не меньше 300×400.

					Проект: Квартира 58 м²
	Лист	№ док.	Подпись	Дата	План выводов сантехники
Дизайнер	Кырлан А.С.			09.10.26	Стадия: П; Лист: 12; Листов: 60


выпуск 09.10.2026 № 7efd137e8f · стр. 12 из 60

Правка к этому листу


План квартиры (М 1:200)

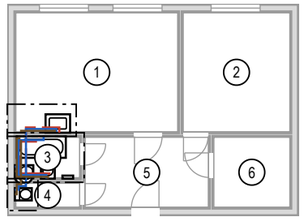


Фр. 1. Кухня-гостиная (М 1:20)

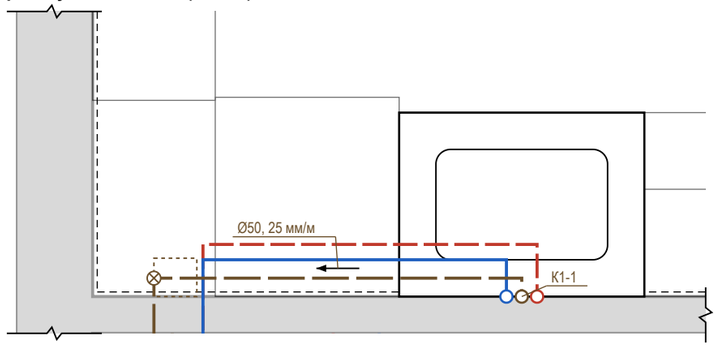

Фр. 2. Ванная (М 1:20)

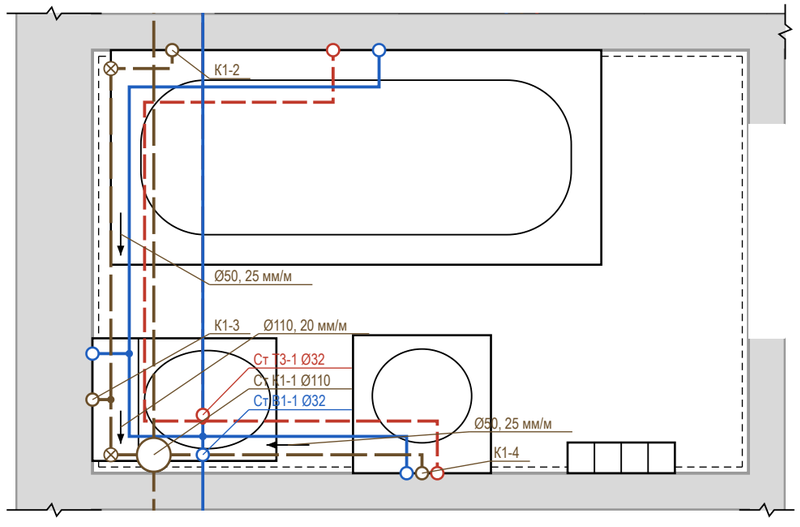

Фр. 3. Санузел (М 1:20)

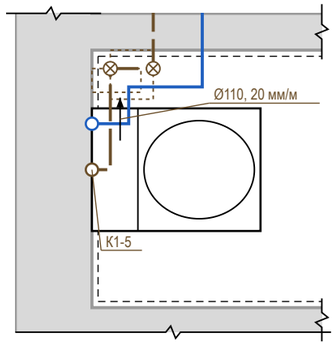

Условные обозначения


- B1 — водопровод хозяйственно-питьевой (ХВС), PP-R Ø20
- Т3 — горячее водоснабжение, подача (ГВС), PP-R Ø20
- К1 — канализация бытовая
- направление уклона К1 / пола: Ø, мм на 1 м
- ревизия (прочистка) К1 — доступ сохранить
- тройник (ответвление к прибору)
- короб К1 над чистым полом (ГКЛВ под плитку)
- вывод В1 (код — в ведомости привязок)
- вывод Т3 (код — в ведомости привязок)
- вывод К1 (код — в ведомости привязок)
- сантехприбор по расстановке (габарит модели)
- стояк «Ст К1-N / Ст В1-N» (ГОСТ 21.601), Ø мм
- линия обрыва (граница фрагмента)
- граница фрагмента на плане (Фр. N)

Профиль выпусков К1 (до врезки в стояк)

Выпуск	Прибор	Ø	L, м	i, мм/м	Δh, мм	Прокладка, мм
К1-5	С_06 унитаз подвесной	Ø110	0,77	20	15	короб 160×140
К1-3	С_03 унитаз подвесной	Ø110	0,38	20	8	в полу: нужно 193 > 90 — решение!
К1-1	С_01 мойка кухонная	Ø50	2,76	25	69	короб 150×110
К1-2	С_02 ванна	Ø50	1,66	25	42	в полу: нужно 167 > 90 — решение!
К1-4	С_04 умывальник	Ø50	0,94	25	23	над полом за приборами

Короб h×b: h — от чистого пола, b — от чистовой стены. Стяжка 90 мм — лист полов.

Узел ввода В1, Т3 (схема, без масштаба)

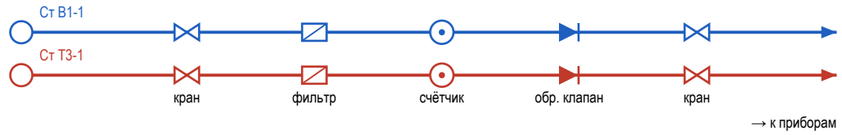

⊗ Ст К1-1: ревизия на стояке — люк в коробе

Примечания

1. Трассы принципиальные, построены от стояков вдоль стен помещений; фактическое положение фиксируется исполнительной схемой с привязками (фото с рулеткой) до закрытия.
2. Уклон К1 не менее 1/d и не более 150 мм/м (СП 30.13330.2020, п. 19.1), приняты практические уклоны; поворот — двумя отводами 45°, ревизия после поворота, доступ сохранить. Стояк К1 в коробе — звукоизоляция стояка в коробе, без жёсткого контакта короба с трубой.
3. Решение по К1: стяжка 90 мм не укрывает трубы (нужно Ø + Δh + 45 мм) — выпуски идут над чистым полом вдоль стен: К1-4 — за приборами и в раме инсталляции; К1-5, К1-1 — в коробе ГКЛВ под плитку (размеры в профиле). Короба — на развёртках; отметку низа врезки в стояк замерить до черновых работ.
4. На каждом вводе В1 и Т3 — кран шаровой, фильтр, счётчик, обратный клапан; доступ через люк не меньше 300×400. Водопровод — в штробе стен или в коробах; трубы испытать давлением до закрытия (акт скрытых работ).
5. Расчёт систем, диаметры магистралей и подбор оборудования выполняет проектная организация; врезка и перенос стояков — по согласованию с управляющей организацией. Арматуру и привязки сверить по паспортам приборов.

					Проект: Квартира 58 м²
	Лист	№ док.	Подпись	Дата	Схема разводки водопровода и канализации
Дизайнер	Кырлан А.С.			09.10.26	

Стадия	Лист	Листов
П	13	60

выпуск 09.10.2026 № 7efd137e8f · стр. 13 из 60

Правка к этому листу

Поз.	Наименование и техническая характеристика	Тип, марка, обозначение документа	Код продукции	Поставщик	Ед. изм.	Кол.	Масса 1 ед., кг	Примечание
	Санитарные приборы							
1	Ванна акриловая 1600×700 мм, с каркасом, экраном и отверстием слив-перелив	Roca Easy ZRU9302899		выбор заказчика	шт	1		С_02
2	Унитаз подвесной безободковый, с сиденьем микролифт, крепёж и звукоизолирующая прокладка	Laufen Pro 8.2096.6.000.000.1		выбор заказчика	шт	2		С_03, С_06
3	Инсталляция для подвесного унитаза: рама высотой 1120 мм, бачок, клавиша смыва (ось клавиши 1050 мм от чистого пола)	аналог		выбор заказчика	шт	2		С_03, С_06; короб ГКЛВ
4	Умывальник подвесной 450×450 мм, с отверстием под смеситель и переливом	Laufen Pro S 8.1096.3.000.104.1		выбор заказчика	шт	1		С_04
5	Мойка кухонная 800×600 мм, с переливом	мойка врезная 780×510 в шкафу М_02		с кухонной мебелью	шт	1		С_01
6	Полотенцесушитель электрический, IP44, с терморегулятором	аналог		выбор заказчика	шт	1		С_05
	Смесители, сифоны и арматура приборов							
7	Смеситель для ванны настенный однорычажный, межосевое 150 мм, с душевым набором (лейка, шланг, держатель)	аналог		выбор заказчика	шт	1		С_02
8	Смеситель для умывальника однорычажный, с донным клапаном	аналог		выбор заказчика	шт	1		С_04
9	Смеситель кухонный однорычажный, высокий излив	аналог		выбор заказчика	шт	1		С_01
10	Обвязка ванны слив-перелив Ø40/50 с сифоном	аналог		выбор заказчика	шт	1		С_02
11	Сифон для умывальника бутылочный Ø32/40–50, с гофрой к выпуску	аналог		выбор заказчика	шт	1		С_04
12	Сифон для мойки Ø40/50	аналог		выбор заказчика	шт	1		С_01
13	Кран угловой ½"×½" с гибкой подводкой 40 см (умывальники, мойка)	аналог		выбор заказчика	шт	4		по 2 на прибор
	Трубопроводы							
14	Труба полипропиленовая PP-R PN20 Ø20×3,4 (В1)	ГОСТ 32415-2013		выбор заказчика	м	11	0,17	6,7 + 3,0 + 10 %
15	Труба PP-R, армированная стекловолокном, PN20 Ø20×2,8 (Т3)	ГОСТ 32415-2013		выбор заказчика	м	8,5	0,15	5,7 + 1,9 + 10 %
16	Труба канализационная ПП Ø50 (К1)	ГОСТ 32414-2013		выбор заказчика	м	7		5,0 + 0,9 + 10 %
17	Труба канализационная ПП Ø110 (К1)	ГОСТ 32414-2013		выбор заказчика	м	2		1,1 + 0,5 + 10 %
	Фасонные части и выводы							
18	Отвод канализационный ПП 45° Ø50	ГОСТ 32414-2013		выбор заказчика	шт	10		2 шт. на поворот
19	Отвод канализационный ПП 45° Ø110	ГОСТ 32414-2013		выбор заказчика	шт	10		2 шт. на поворот
20	Тройник канализационный ПП 45° (врезки ветвей)	ГОСТ 32414-2013		выбор заказчика	шт	4		
21	Ревизия канализационная ПП (после поворота трассы)	ГОСТ 32414-2013		выбор заказчика	шт	5		доступ сохранить
22	Фитинги PP-R Ø20: тройники, угольники 90° (ветви и повороты В1, Т3)	ГОСТ 32415-2013		выбор заказчика	шт	22		
23	Водорозетка PP-R Ø20×½" настенная, с креплением	ГОСТ 32415-2013		выбор заказчика	шт	8		коды — лист выводов
	Узлы ввода, люки, короба							
24	Кран шаровой латунный Ду15 PN16 (отключение ввода)	аналог		выбор заказчика	шт	2		Ст В1-1, Ст Т3-1
25	Фильтр сетчатый косой Ду15	аналог		выбор заказчика	шт	2		
26	Счётчик воды крыльчатый Ду15 (ХВ, ГВ), с поверкой	аналог		выбор заказчика	шт	2		пломба УК
27	Клапан обратный Ду15	аналог		выбор заказчика	шт	2		
28	Люк ревизионный нажимной под плитку 300×400 мм	аналог		выбор заказчика	шт	1		к стоякам и арматуре
29	Звукоизоляция стояка К1 в коробе: рулонный звукоизоляционный материал ≥ 10 мм, обмотка стояка на высоту этажа	аналог		выбор заказчика	м	2,7		Ст К1-1
30	Короб К1 над полом: профиль ПН/ПС, ГКЛВ 12,5 мм под плитку	аналог		выбор заказчика	м	0,6		сечение — лист разводки

Примечания

1. Форма 1 ГОСТ 21.110-2013, ширины граф изменены по п. 4.1. «Аналог» — аналог по характеристикам: модели внести до черновых работ, привязки выводов сверить по паспортам.
2. Бытовая техника не входит (показана арматура подключения), мойка — в комплекте кухни. Длины труб — трасса листа разводки + подъёмы + 10 %.
3. Стояк К1 в коробе — звукоизоляция стояка в коробе без жёсткого контакта короба с трубой.
4. Расчёт систем водоснабжения и канализации, диаметры магистралей и подбор оборудования выполняет проектная организация.

					Проект: Квартира 58 м²
	Лист	№ док.	Подпись	Дата	Спецификация сантехнического оборудования
Дизайнер	Кырлан А.С.			09.10.26	


Стадия	Лист	Листов
П	14	60

выпуск 09.10.2026 № 7efd137e8f · стр. 14 из 60

Правка к этому листу

Примечания

1. Размеры проёмов и привязки — в миллиметрах от чистых граней стен до отделки; привязка — от угла того помещения, со стороны которого стоит размер. Размер в ведомости — ширина × высота проёма от чистого пола 0,000. Откос от угла помещения до проёма с коробкой — не менее 50 мм.
2. Марки в кружках — типы заполнения проёмов (ГОСТ 21.501-2018, п. 5.3.2); одна марка — один типоразмер; количество сверено с планом.
3. Открывание: Л — петли слева, П — справа, если смотреть со стороны, куда открывается полотно (на себя).
4. Скрытые двери (Д-2…Д-4): проём замерить в чистоте; блок заказать до штукатурки (≈ 30 дн.), короб ставить до штукатурки; полотно навесить после чистовой отделки, красить в цвет стен. Порядок практика монтажа, изготовитель подтверждает.
5. Д-2…Д-4 — существующие проёмы, до техзаключения не расширять.
6. Экспликация помещений — лист 3; в марках помещений — номер и площадь, м².
7. Привязка проёма к углу помещения меньше 1 мм на листе, размер на плане не показан: Д-3 — 40 мм; Д-4 — 40 мм.

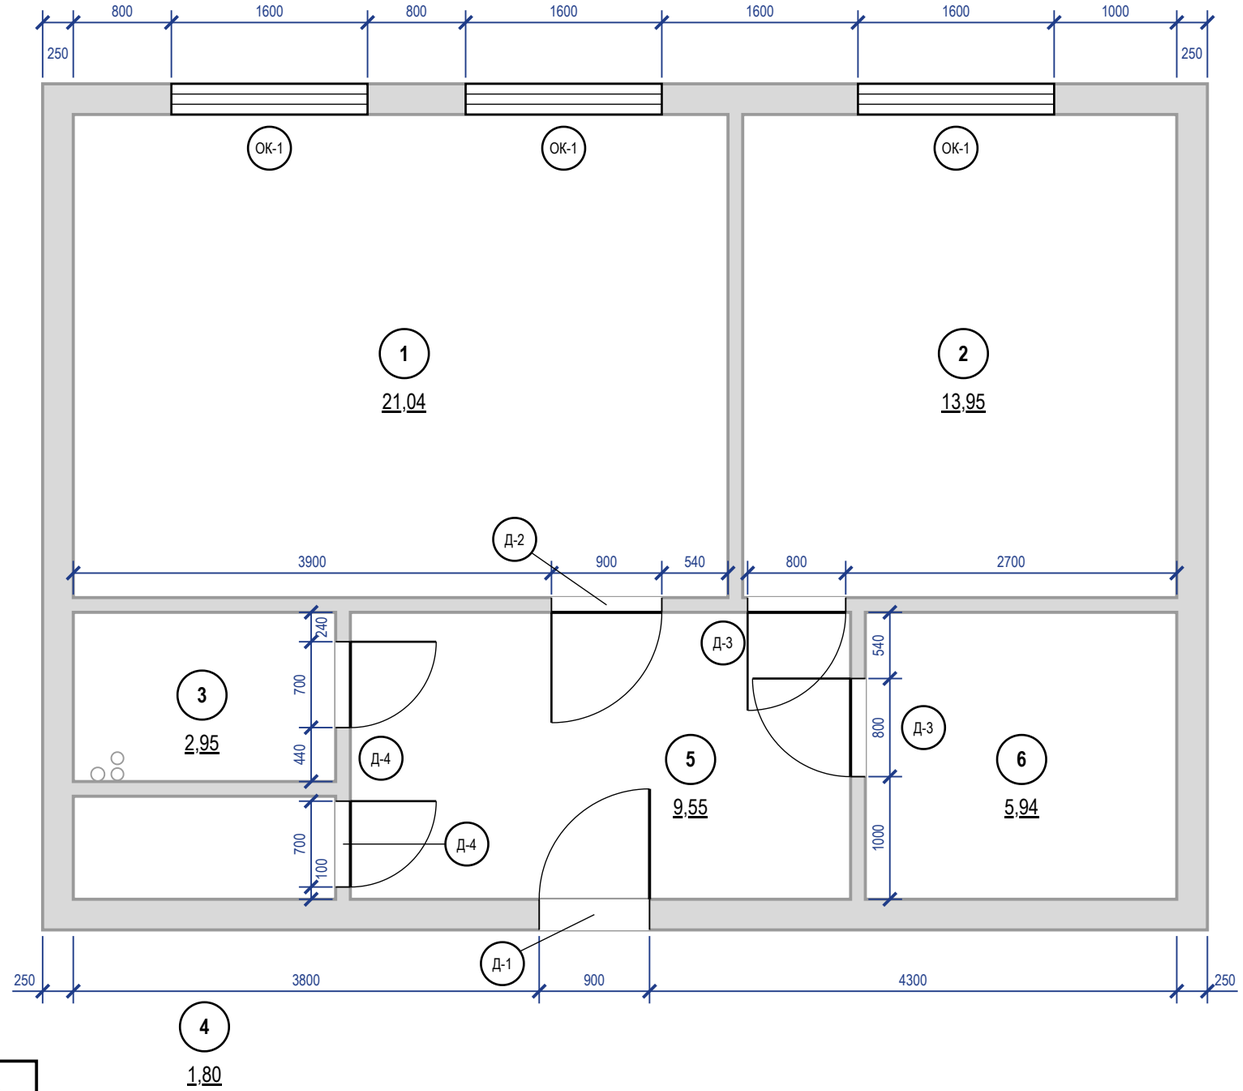

4
1,80


Ведомость заполнения проёмов

Марка	Наименование, обозначение	Проём ш×в, мм	Кол.	Откр.	Отделка полотна	Фурнитура	Прим.
Д-1	Блок дверной входной, ГОСТ 31173-2016	900×2100	1	Л	в комплекте блока	в комплекте блока (замки, глазок)	
Д-2	Дверь скрытого монтажа, ТУ изготовителя	900×2100	1	Л	S 1502-Y50R — пом. 5, S 1002-Y50R — пом. 1	скрытые петли 3D, магнитный замок	
Д-3	Дверь скрытого монтажа, ТУ изготовителя	800×2100	2	Л, Л	окраска S 1502-Y50R с двух сторон; S 1502-Y50R — пом. 5, V503 — пом. 6	скрытые петли 3D, магнитный замок	
Д-4	Дверь скрытого монтажа, ТУ изготовителя	700×2100	2	П, П	S 1502-Y50R — пом. 5, в тон облицовки — пом. 3; S 1502-Y50R — пом. 5, в тон облицовки — пом. 4	скрытые петли 3D, магнитный замок, фиксатор WC	порог 15
ОК-1	Блок оконный, ГОСТ 23166-2021	1600×1600	3				низ 800

					Проект: Квартира 58 м²			
	Лист	№ док.	Подпись	Дата	План размещения дверей	Стадия	Лист	Листов
Дизайнер	Кырлан А.С.			09.10.26		П	15	60

выпуск 09.10.2026 № 7efd137e8f · стр. 15 из 60

Правка к этому листу

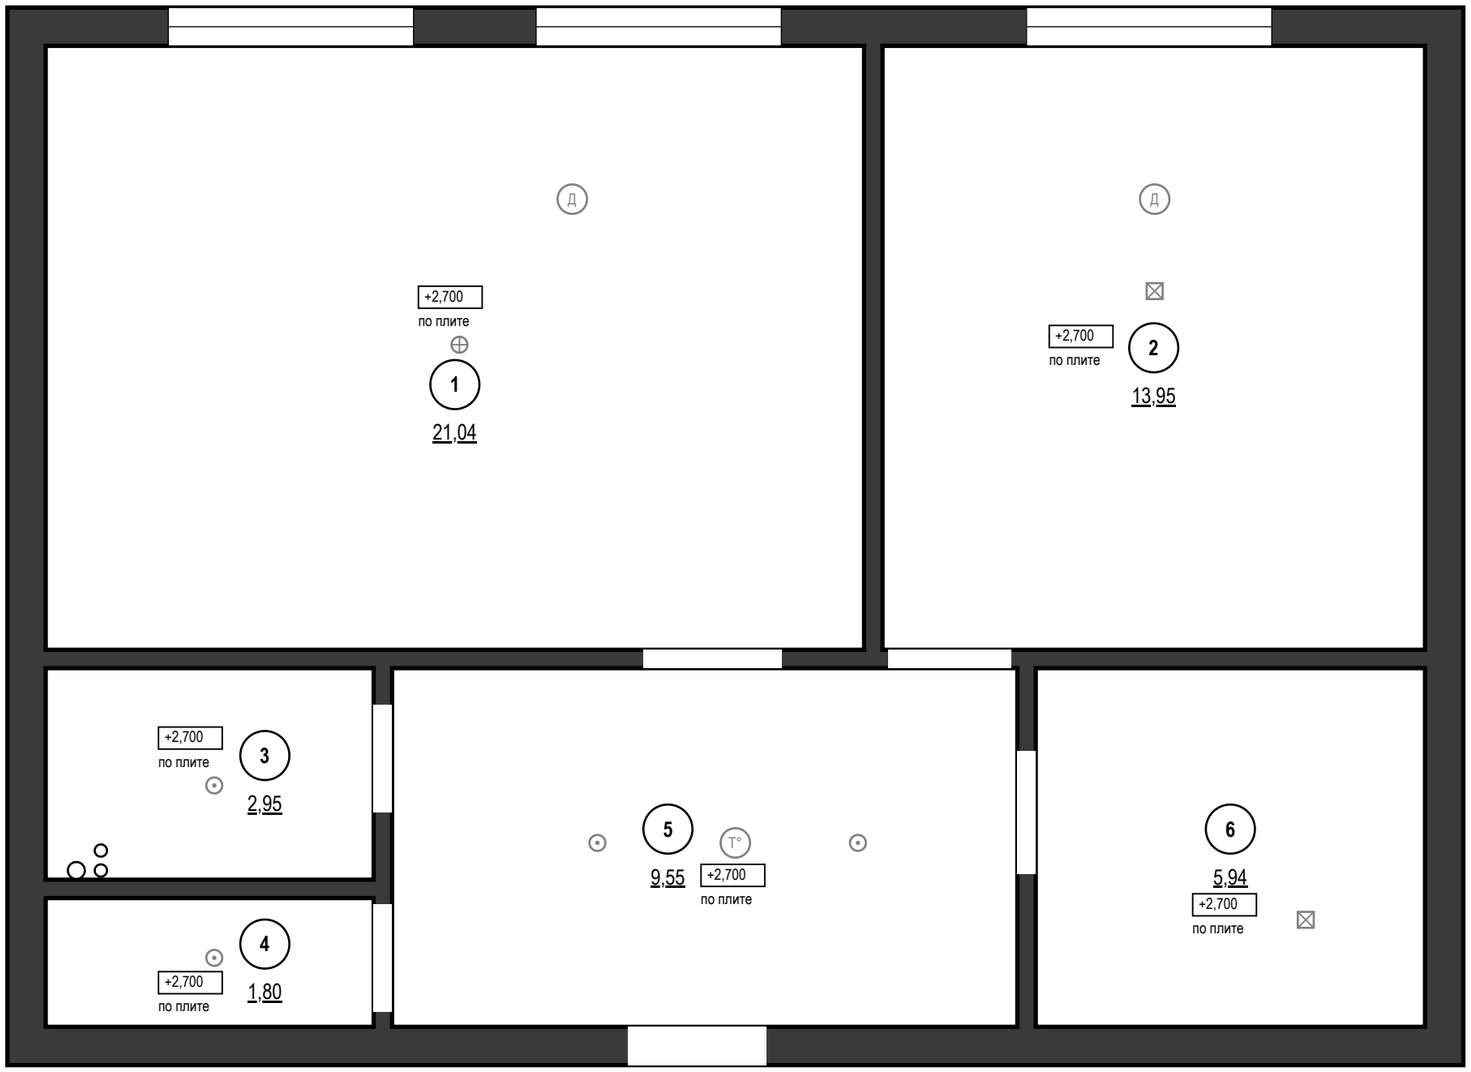

Ведомость потолков

Пом.	Марка	Конструкция	Низ	S, м²	Q
1		по плите, окраска	+2,700	21,04	
2		по плите, окраска	+2,700	13,95	
3		по плите, окраска	+2,700	2,95	
4		по плите, окраска	+2,700	1,80	
5		по плите, окраска	+2,700	9,55	
6		по плите, окраска	+2,700	5,94	
		Итого		**55,23**	

Ведомость вырезов и закладных в потолке

Марка	Устройство	Кол.	Пом.
	Светильник встраиваемый (марки — план освещения)	4	3, 4, 5
	Светильник накладной (марки — план освещения)	2	2, 6
	Светильник подвесной (марки — план освещения)	1	1
	Извещатель дымовой	2	1, 2
	Извещатель тепловой	1	5

Примечания


1. За отметку ±0,000 принят уровень чистого пола сухих помещений (готовое покрытие), а не существующего пола; пол пом. 3, 4 — −0,015; верх плиты перекрытия −0,064 — расчётный по пирогу пола, не замерен; существующий пол снимается до плиты, его отметка не замерена. Отметки в прямоугольниках — низ потолка; низ плиты перекрытия +2,700. Марка потолка — одна конструкция и отметка на весь альбом.
2. Светильники и потолочные устройства — подложка с планов освещения, слаботочных систем и вентиляции (положение — по ним); вырезы и закладные — по ведомости на листе, до обшивки; отверстия не совмещать с профилями.
3. Пом. 1, 2, 3, 4, 5, 6 — потолок по плите без подвесной системы; отделка — по ведомости отделки.

					Проект: Квартира 58 м²
	Лист	№ док.	Подпись	Дата	План потолков
Дизайнер	Кырлан А.С.			09.10.26	

Стадия	Лист	Листов
П	16	60

выпуск 09.10.2026 № 7efd137e8f · стр. 16 из 60

Правка к этому листу

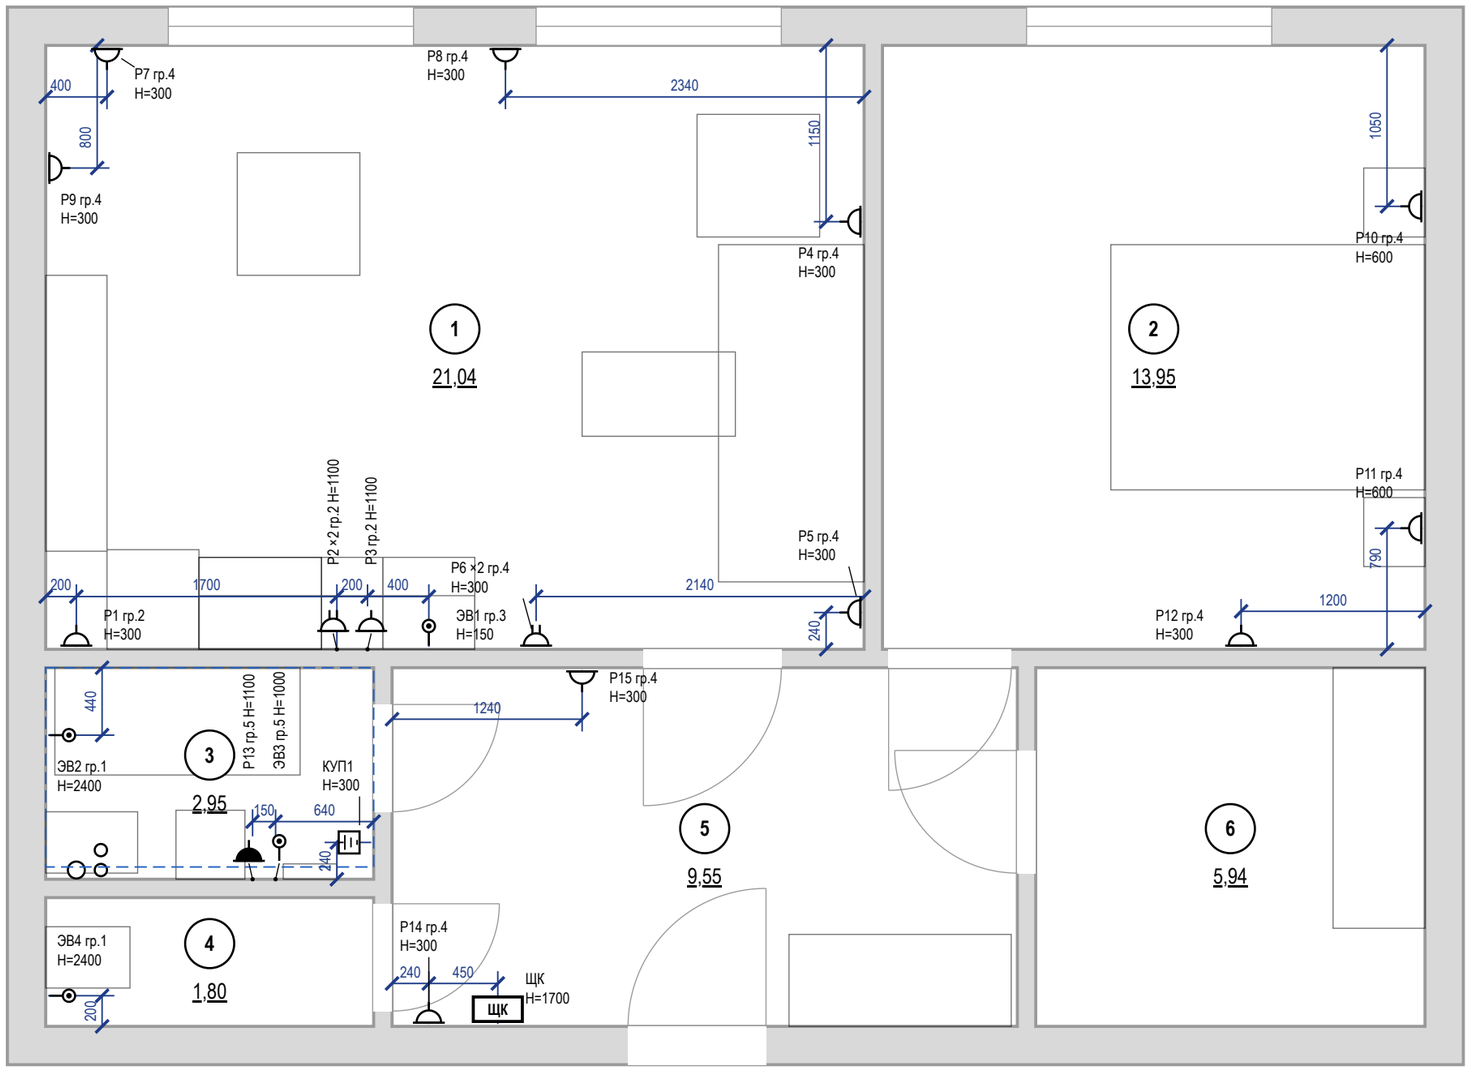

Условные обозначения


- розетка с заземляющим контактом; у знака — марка, ×N постов в рамке, гр. — группа щита, H — высота оси, мм
- то же, рамка на 2 поста (число черточек — число постов)
- розетка влагозащищённая IP44
- вывод кабеля для подключения прибора (без розетки), марка ЭВ
- КУП — коробка уравнивания потенциалов (ДСУП), проводник к шине PE щита
- ЩК — щит квартирный
- знак разведён для читаемости: точка на стене — у выноски, привязка — до неё
- граница зоны 2 ванной (600 мм от ванны/поддона)
- мебель и сантехприборы — подложка
- стояк: К1 — канализация, В1 — ХВС, Т3 — ГВС
- 1 — номер помещения, площадь м²

Примечания

1. За отметку 0,000 принят уровень чистого пола. Высоты H — от чистого пола до оси изделия; привязки — от чистовой грани стены до оси механизма (у рамки на несколько постов — до оси рамки).
2. Высота установки, не указанная на плане: розетки — 300 мм от чистого пола; выводы кабеля — по паспорту прибора.
3. Розетки в санузле — только вне зон 0–2 (ПУЭ 7.1.48, ГОСТ Р 50571.7.701-2024), IP44, через УЗО 30 мА.
4. Розеточные и мокрые линии — через УЗО или дифавтомат с током утечки не более 30 мА (ПУЭ 7.1.79); в санузле выполнить ДСУП (ПУЭ 7.1.87–7.1.88).
5. Кабель — медный, исполнение нг(A)-LS (ГОСТ 31565-2012); скрытая прокладка только горизонтально и вертикально, фактические трассы зафиксировать исполнительной схемой до закрытия отделкой.
6. Расчёт нагрузок, токов КЗ, селективности и сечений — по проекту ЭОМ организации с допуском СРО; лист задаёт состав, расположение и группы.
7. Выводы кухонной техники — после утверждения проекта кухни (ориентировочно); привязки выводов даны от осей модулей гарнитура и пересматриваются вместе с проектом кухни.
8. Ведомости электроточек, изделий, светильников и расшифровка клавиш — лист «Ведомость электроточек и изделий».

					Проект: Квартира 58 м²			
	Лист	№ док.	Подпись	Дата	План розеток и электровыводов	Стадия	Лист	Листов
Дизайнер	Кырлан А.С.			09.10.26		П	17	60

Правка к этому листу

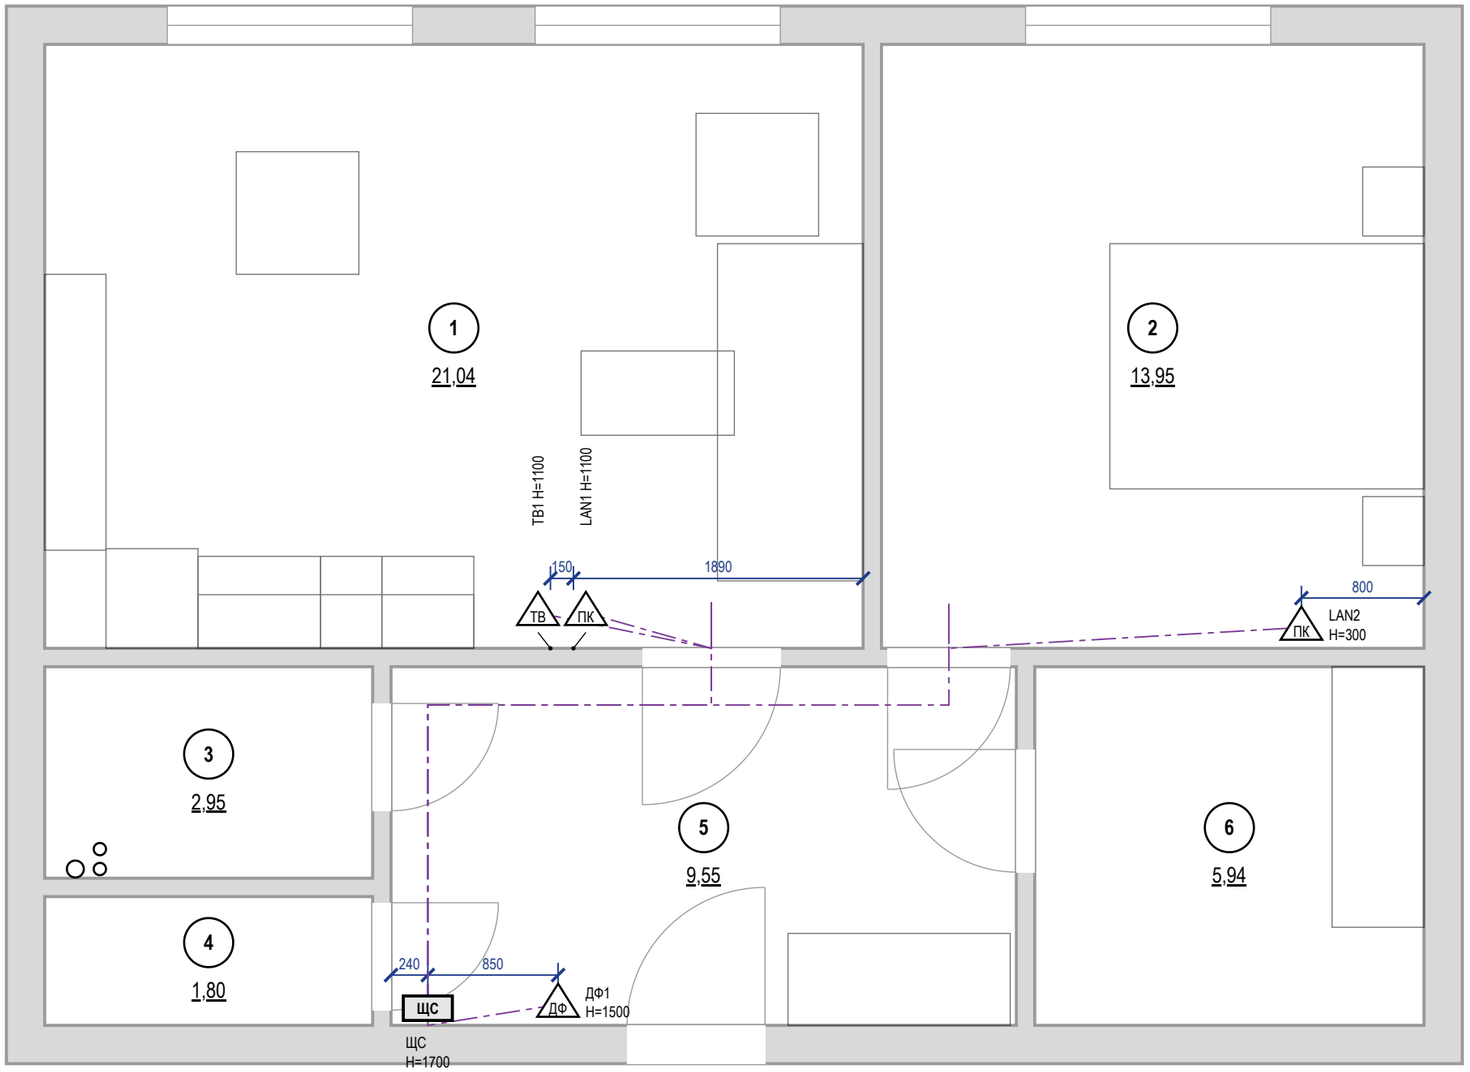


Примечания

1. За отметку 0,000 принят уровень чистого пола. Высоты Н — от чистого пола до оси изделия; привязки — от чистовой грани стены до оси механизма (у рамки на несколько постов — до оси рамки).
2. Высота установки, не указанная на плане: розетки LAN и ТВ — 300 мм от чистого пола.
3. Слаботочные кабели — отдельно от силовых: в своей трубе или лотке, при параллельной прокладке не ближе 100 мм к силовым, пересечения под прямым углом; каждую точку — отдельным кабелем от ЩС без скруток.
4. Трассы на листе — принципиальные; фактические зафиксировать исполнительной схемой до закрытия отделкой. Силовые линии, УЗО 30 мА, ДСУП, кабель нг(А)-LS — по листам розеток и щита.
5. Проект силовой части и расчёт токов КЗ — по проекту ЭОМ; слаботочная часть согласуется с провайдером и управляющей компанией (домофон, коллективное ТВ).

					Проект: Квартира 58 м²
	Лист	№ док.	Подпись	Дата	
Дизайнер	Кырлан А.С.			09.10.26	План слаботочных сетей
					Стадия: П; Лист: 18; Листов: 60

выпуск 09.10.2026 № 7efd137e8f · стр. 18 из 60

Правка к этому листу

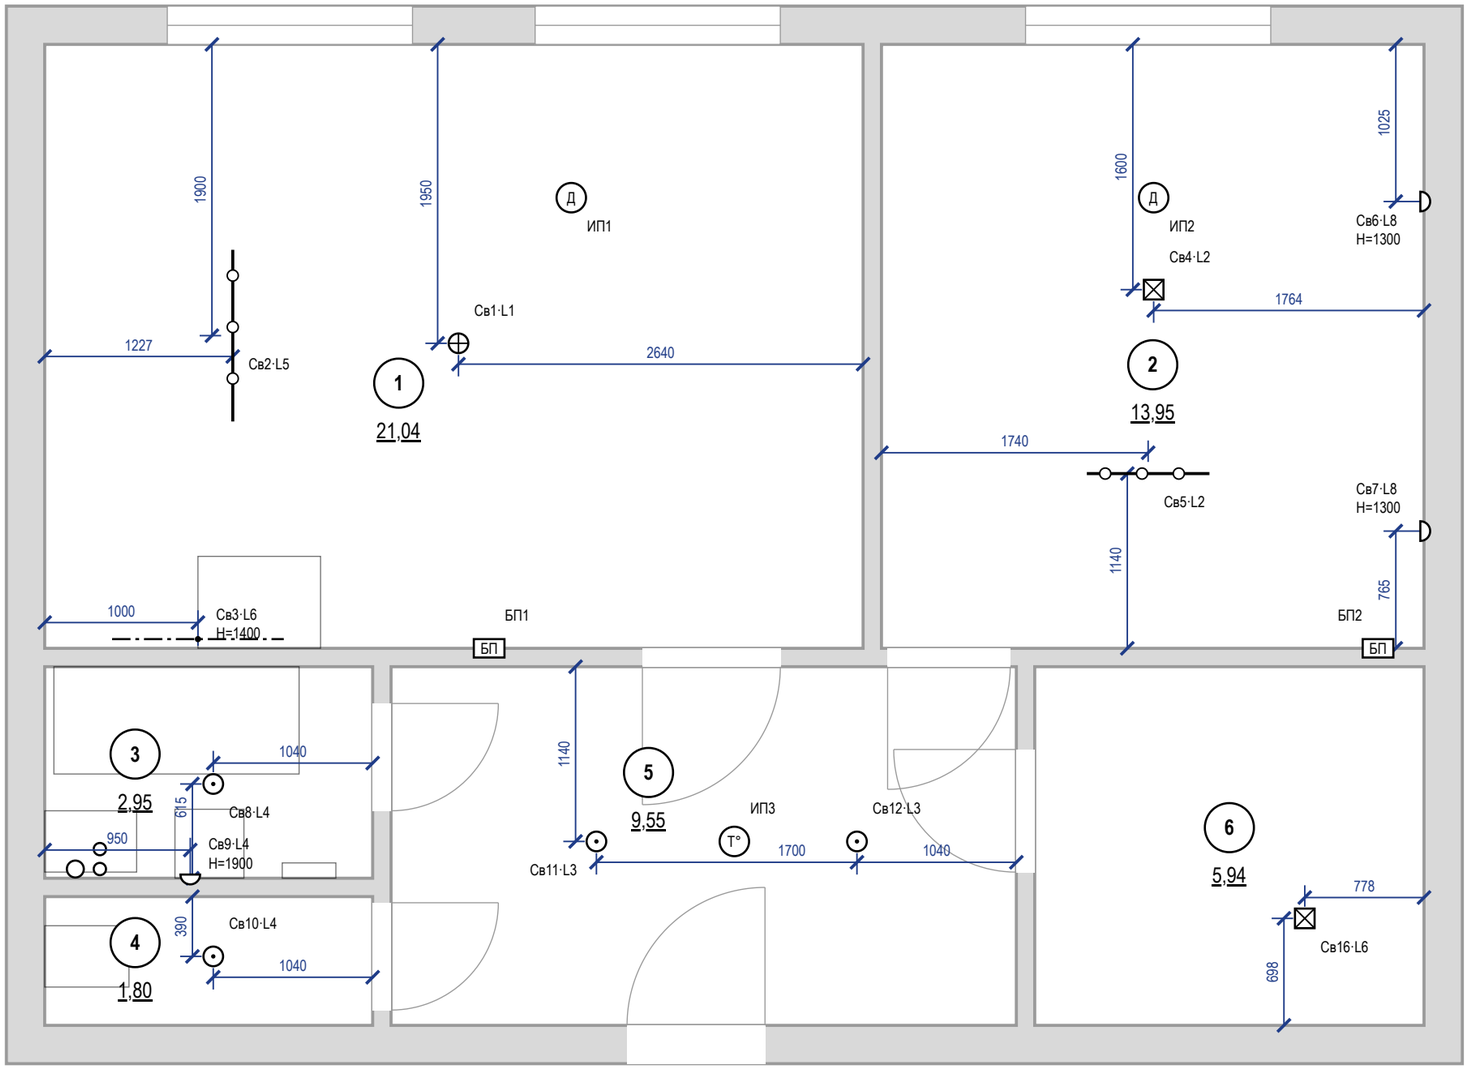

Примечания

1. За отметку 0,000 принят уровень чистого пола. Высоты H — от чистого пола до оси изделия; привязки — от чистовой грани стены до оси механизма (у рамки на несколько постов — до оси рамки).
2. Высота установки, не указанная на плане: светильники — на потолке; настенные — по отметке H у знака. Привязки — до оси светильника от чистовой грани стены, по рядам.
3. Освещённость: Ен — СанПиН 1.2.3685-21, табл. 5.52 (на полу); Ф треб. = Ен·S/(U·MF) при U = 0,5 и MF = 0,71 (СП 52.13330.2016, табл. 4.3) — оценка, не светотехнический расчёт. Декоративная подсветка в Ф не входит.
4. Во влажных помещениях — светильники не ниже IP44; в зонах 0–2 ванной — по ГОСТ Р 50571.7.701-2024 (зона 1 — IPX5).
5. Розеточные и мокрые линии — через УЗО или дифавтомат с током утечки не более 30 мА (ПУЭ 7.1.79); в санузле выполнить ДСУП (ПУЭ 7.1.87–7.1.88).
6. Кабель — медный, исполнение нг(A)-LS (ГОСТ 31565-2012); скрытая прокладка только горизонтально и вертикально, фактические трассы зафиксировать исполнительной схемой до закрытия отделкой.
7. Расчёт нагрузок, токов КЗ, селективности и сечений — по проекту ЭОМ организации с допуском СРО; лист задаёт состав, расположение и группы.
8. Ведомость светильников — лист «Ведомость электроточек и изделий».

					Проект: Квартира 58 м²
	Лист	№ док.	Подпись	Дата	План освещения
Дизайнер	Кырлан А.С.			09.10.26	Стадия: П; Лист: 19; Листов: 60

Правка к этому листу

Спецификация светильников

Поз.	Марки	Наименование	Установка	Кол.	P, Вт	Σ P, Вт	Ф, лм	Тц, К	Ra	Угол, °	IP	Дим.	Группа	Пом.
1	Св1	Подвесной	подвес	1	40	40	3600	3000	90	—	20	—	L1	1
2	Св2	Трековая система	на потолке	4	12	48	950	3000	90	—	20	—	L5	1
3	Св3	Линейный настенный	под верхними шкафами, H=1400	1	14	14	1080	3000	90	—	20	—	L6	1
4	Св4	Потолочный накладной	на потолке	1	36	36	3200	2700	90	—	20	—	L2	2
5	Св5	Трековая система	на потолке	2	12	24	900	2700	90	—	20	—	L2	2
6	Св6, Св7	Настенный (бра)	на стене, H=1300	2	4	8	250	2700	90	—	20	—	L8	2
7	Св8	Встраиваемый точечный	встраиваемый	1	9	9	700	3000	90	—	44	—	L4	3
8	Св9	Настенный (бра)	над зеркалом, H=1900	1	6	6	400	3000	90	—	44	—	L4	3
9	Св10	Встраиваемый точечный	встраиваемый	1	6	6	500	3000	90	—	44	—	L4	4
10	Св11, Св12	Встраиваемый точечный	встраиваемый	2	9	18	800	3000	90	—	20	—	L3	5
11	Св16	Потолочный накладной	на потолке, засветка стены	1	10	10	900	3000	90	—	20	—	L6	6
		Итого		**17 шт**		**219**								

Слои света по помещениям

Пом.	Помещение	Слои света и группы включения (марки светильников)	Тц, К	Ra	Σ P, Вт	Сцен.
1	Кухня-гостиная	общий — L1 (Св1), L5 (Св2); рабочий — L6 (Св3)	3000	90	102	—
2	Спальня	общий — L2 (Св4, Св5); рабочий — L8 (Св6, Св7)	2700	90	68	—
3	Ванная	общий — L4 (Св8); рабочий — L4 (Св9)	3000	90	15	—
4	Санузел	общий — L4 (Св10)	3000	90	6	—
5	Прихожая	общий — L3 (Св11, Св12)	3000	90	18	—
6	Гардеробная	общий — L6 (Св16)	3000	90	10	—

LED-ленты, линейные светильники и блоки питания

Марка	Пом.	L, м	U, В	Вт/м	Σ P, Вт	БП	P БП, Вт	Загр., %	Питание	Доступ к БП
Св2	1	1,2	24	—	48	БП1	100	62	встроенный ввод	H=2300
—	1	1,8	24	—	14	БП1	100	62	встроенный ввод	H=2300
Св5	2	0,8	24	—	24	БП2	60	40	встроенный ввод	H=2300

Сценарии освещения

Сценарии не заданы: группы включаются клавишами по плану выключателей (лист 21).

Слои света

общий — равномерный свет помещения, по норме освещённости


рабочий — местный свет задачи: столешница, зеркало, чтение у кровати

Примечания

1. Позиции и марки Св — те же, что на плане освещения (лист 19) и в ведомости светильников (лист «Ведомость электроточек и изделий»); группы L — по плану выключателей (лист 21).
2. Модели светильников не назначены: подбор по графам спецификации — поток, Тц, Ra, угол, IP и диммирование не хуже указанных, мощность не больше. IP 20 — сухие помещения.
3. Мощность и поток — по паспортам принятых изделий, Σ P — установленная мощность освещения. Оценка освещённости — на плане освещения; это не светотехнический расчёт.

					Проект: Квартира 58 м²			
	Лист	№ док.	Подпись	Дата	Спецификация светильников и сценарии освещения	Стадия	Лист	Листов
Дизайнер	Кырлан А.С.			09.10.26		П	20	60


Правка к этому листу

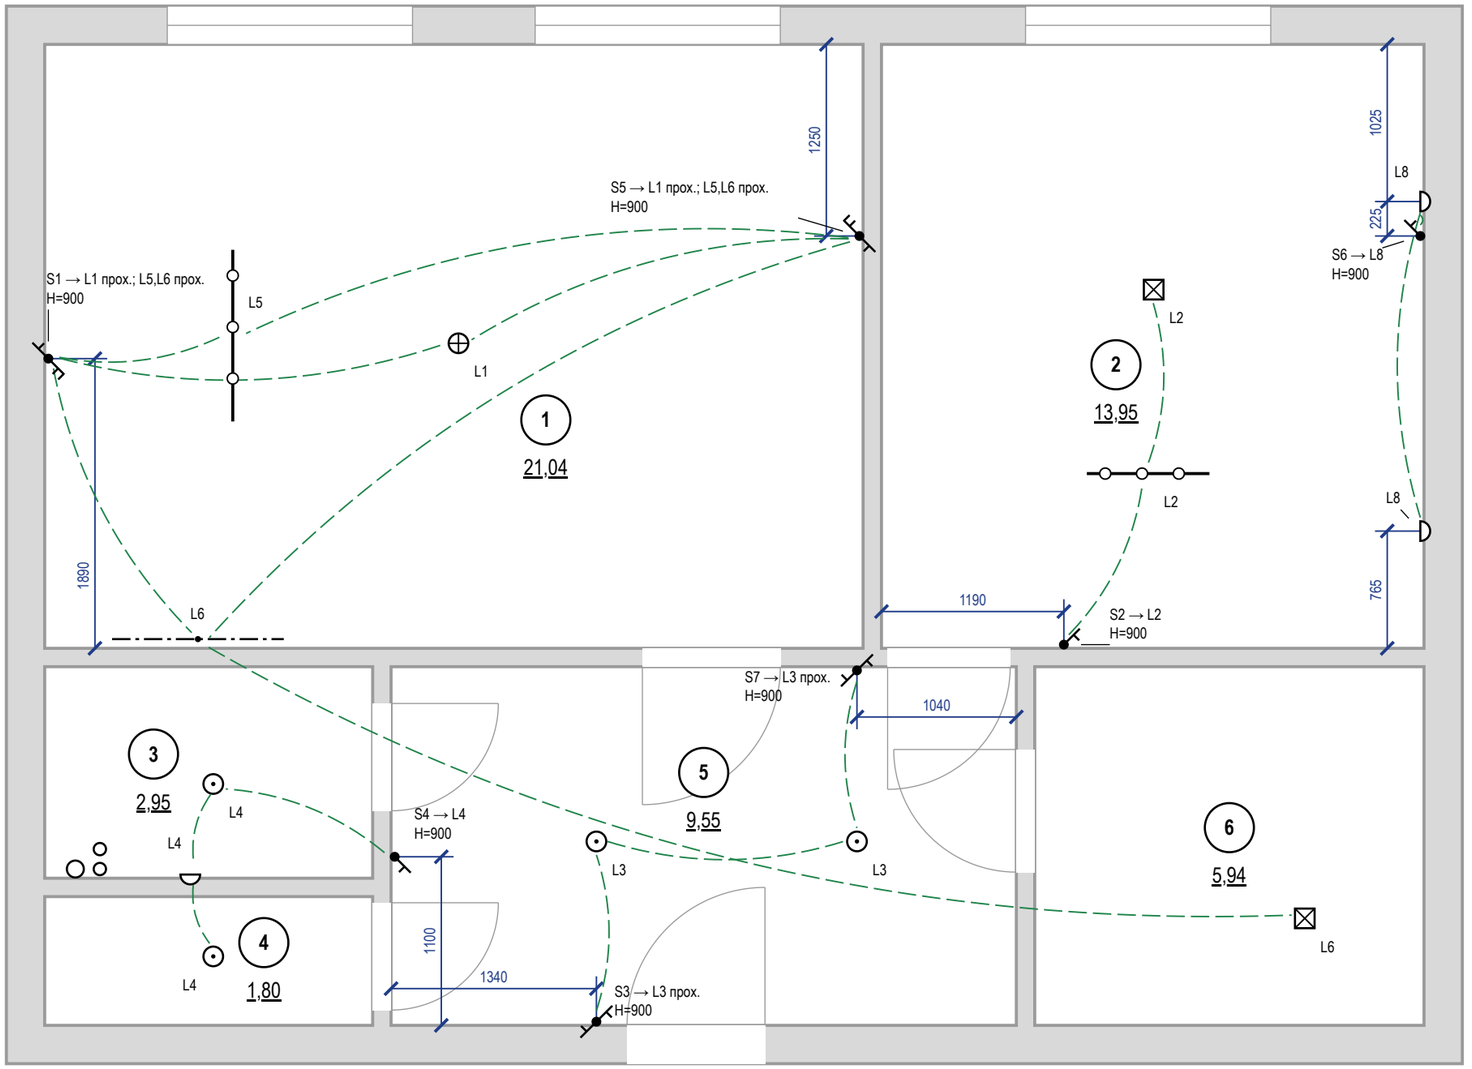

Примечания

1. За отметку 0,000 принят уровень чистого пола. Высоты H — от чистого пола до оси изделия; привязки — от чистовой грани стены до оси механизма (у рамки на несколько постов — до оси рамки).
2. Высота установки, не указанная на плане: выключатели — 900 мм от чистого пола, со стороны дверной ручки (ПУЭ 7.1.51).
3. Линии связи показывают, какой выключатель какую группу L включает; это не трасса кабеля. Трасса — принципиальная, фактическую зафиксировать исполнительной схемой.
4. Группы из нескольких мест (L1 — S1, S5; L5 — S1, S5; L6 — S1, S5; L3 — S3, S7): на крайних местах — проходные клавиши, на промежуточных — перекрёстные; механизмы — в ведомости изделий.
5. Вентиляторы санузлов (выводы ЭВ на плане розеток) включаются вместе с основным светом помещения, отключаются с задержкой — таймер выбега в вентиляторе.
6. Розеточные и мокрые линии — через УЗО или дифавтомат с током утечки не более 30 мА (ПУЭ 7.1.79); в санузле выполнить ДСУП (ПУЭ 7.1.87–7.1.88).
7. Кабель — медный, исполнение нг(A)-LS (ГОСТ 31565-2012); скрытая прокладка только горизонтально и вертикально, фактические трассы зафиксировать исполнительной схемой до закрытия отделкой.
8. Расчёт нагрузок, токов КЗ, селективности и сечений — по проекту ЭОМ организации с допуском СРО; лист задаёт состав, расположение и группы.
9. Расшифровка клавиш и ведомость изделий — лист «Ведомость электроточек и изделий».

					Проект: Квартира 58 м²
	Лист	№ док.	Подпись	Дата	Управление светильниками
Дизайнер	Кырлан А.С.			09.10.26	Стадия: П; Лист: 21; Листов: 60

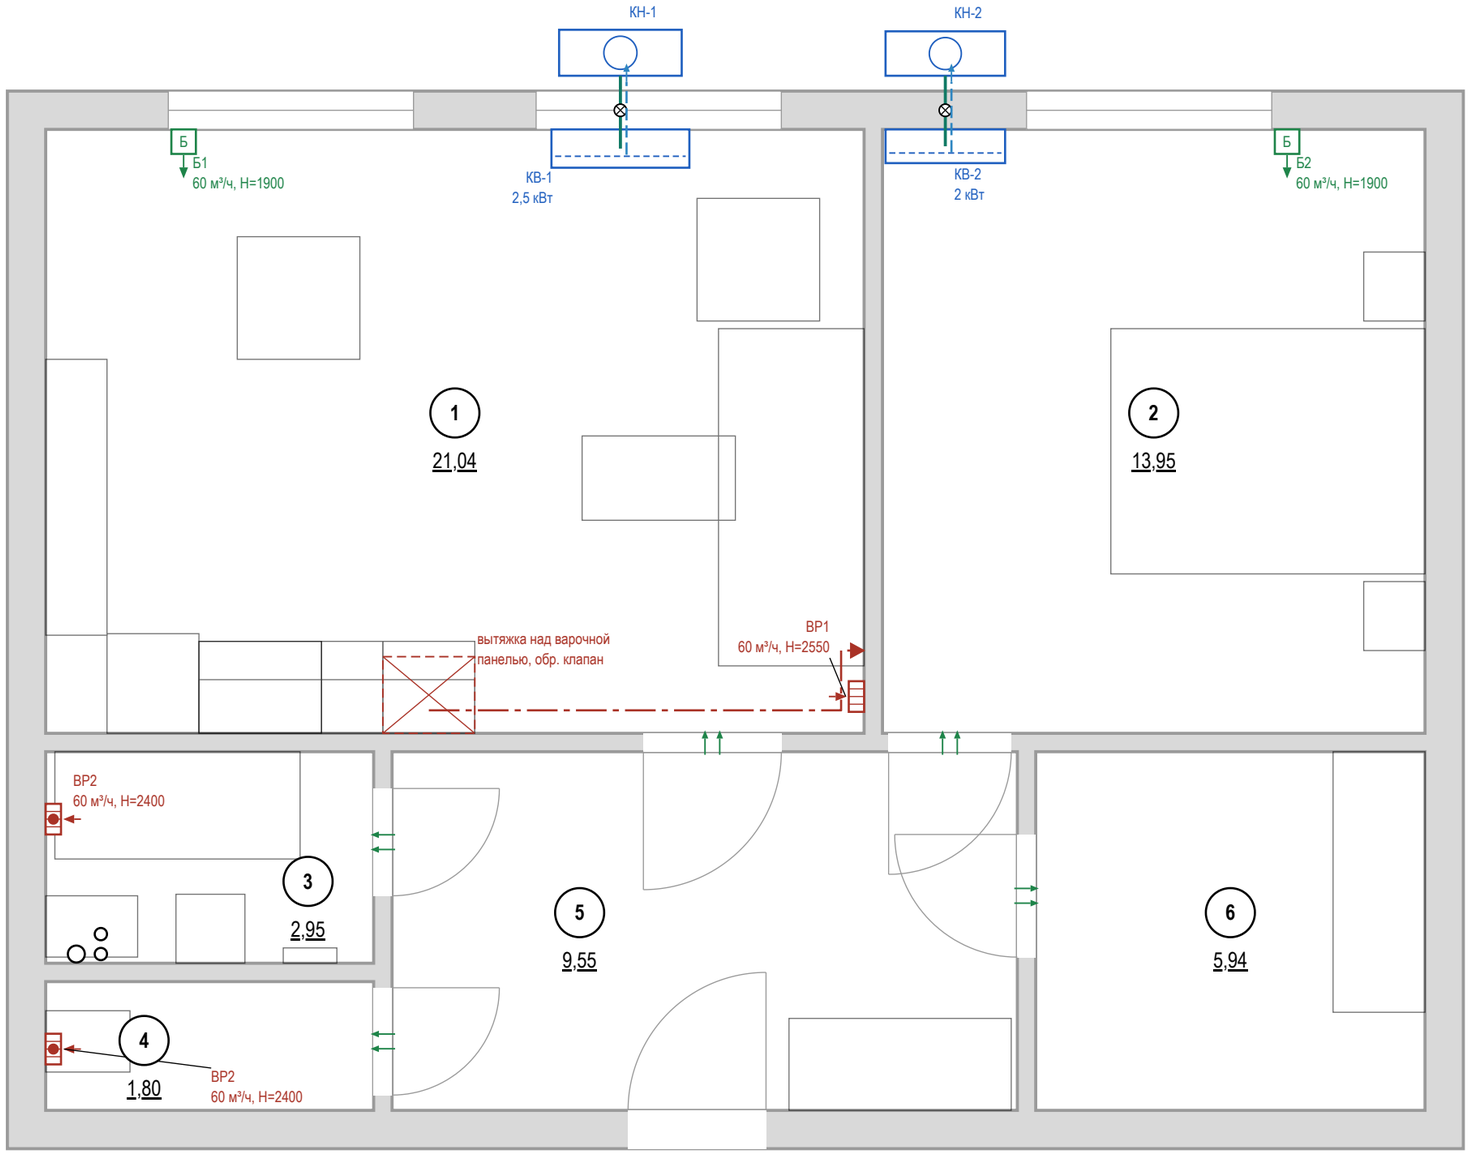

Условные обозначения

- стояк: К1 — канализация, В1 — ХВС, Т3 — ГВС
- номер помещения, площадь м²
- вытяжная решётка в вентканал: марка, расход м³/ч, Н центра от чистого пола
- вытяжная решётка с бытовым вентилятором и обратным клапаном: марка, расход, Н
- бризер (приток с фильтром и подогревом)
- переток: зазор под полотном или переточная решётка
- кухонная вытяжка над варочной панелью
- воздуховод кухонной вытяжки в коробе под потолком
- отдельный вход воздуховода в вентканал, обратный клапан
- внутренний блок кондиционера (КВ-N)
- наружный блок (КН-N) на фасаде / в корзине
- трасса фреонопровода и межблочного кабеля
- дренаж конденсата (уклон стрелкой)
- отверстие в наружной стене под трассу

Воздухообмен, м³/ч

№	Помещение	Выт. норма	Выт. проект	Прит. норма	Прит. проект	Устройства
1	Кухня-гостиная	60	60	60	60	ВР1, Б1
2	Спальня			60	60	Б2
3	Ванная	50	60			ВР2
4	Санузел	25	60			ВР2
6	Гардеробная	3				переток
	Итого	**138**	**180**	**60**	**120**	

Воздухообмен квартиры — по большей из сумм притока и вытяжки: норма 138 м³/ч, проект 180 м³/ч.
Вытяжка не меньше притока — баланс сведён.

Кондиционеры

Марка	Помещение	Нар. блок	Трасса, м	Дренаж
КВ-1	1. Кухня-гостиная	КН-1	3,0 п	наружу, i=50 мм/м
КВ-2	2. Спальня	КН-2	3,0 п	наружу, i=50 мм/м

Примечания


1. Расчёт систем ОВ и подбор оборудования — проектная организация с допуском СРО; лист даёт места, трассы и привязки.
2. Нормы вытяжки — СП 54.13330.2022 (Изм. 1, 2), табл. 7.1: кухня с электроплитой 60 м³/ч, с газовой 100; ванная и совмещённый санузел 50; уборная 25; гардеробная 0,2 ч⁻¹. Приток в жилые — 3 м³/ч на 1 м² (менее 20 м² общей площади на человека), иначе 30 м³/ч на человека.
3. Вентканалы и шахты не сужать, не переносить и не закрывать; вентилятор и кухонная вытяжка — через обратный клапан, без перекрытия естественной тяги.
4. Кухонная вытяжка в воздухообмен не включена: воздуховод не менее Ø125 в коробе, вход в канал отдельный.
5. Переток — зазор под полотнами межкомнатных дверей или переточная решётка.
6. Дренаж кондиционера — непрерывный уклон 40–60 мм/м без контруклонов (СТО НОСТРОЙ 2.23.1-2011, п. 5.8.4); врезка в К1 — через сифон (п. 5.8.9); длина трассы и перепад высот — по паспорту блока; внутренний блок — не ближе 150 мм к потолку, не над кроватью и рабочим местом.
7. Наружный блок на фасаде многоквартирного дома — с согласия собственников (общее имущество); при наличии корзин — только в них.
8. «п» в графе «Трасса» — трасса фреона по плану короче минимума, разница выбрана компенсационной петлёй (бухтой): КВ-1 — по плану 0,8 м, с петлёй 3,0 м; КВ-2 — по плану 0,8 м, с петлёй 3,0 м. Длина петли принята по минимуму трассы (3,0 м) и зависит от паспорта модели кондиционера, которая ещё не выбрана: минимум и максимум трассы — типовые, по паспорту модели, до заказа сверить и при необходимости изменить петлю или место наружного блока. Бухту уложить в коробе или за внутренним блоком, не в штробе.
9. Привязки оборудования — по паспортам приобретённых моделей, до черновых работ.

					Проект: Квартира 58 м²
	Лист	№ док.	Подпись	Дата	План вентиляции
Дизайнер	Кырлан А.С.			09.10.26	

Стадия	Лист	Листов
П	22	60

выпуск 09.10.2026 № 7efd137e8f · стр. 22 из 60

Правка к этому листу

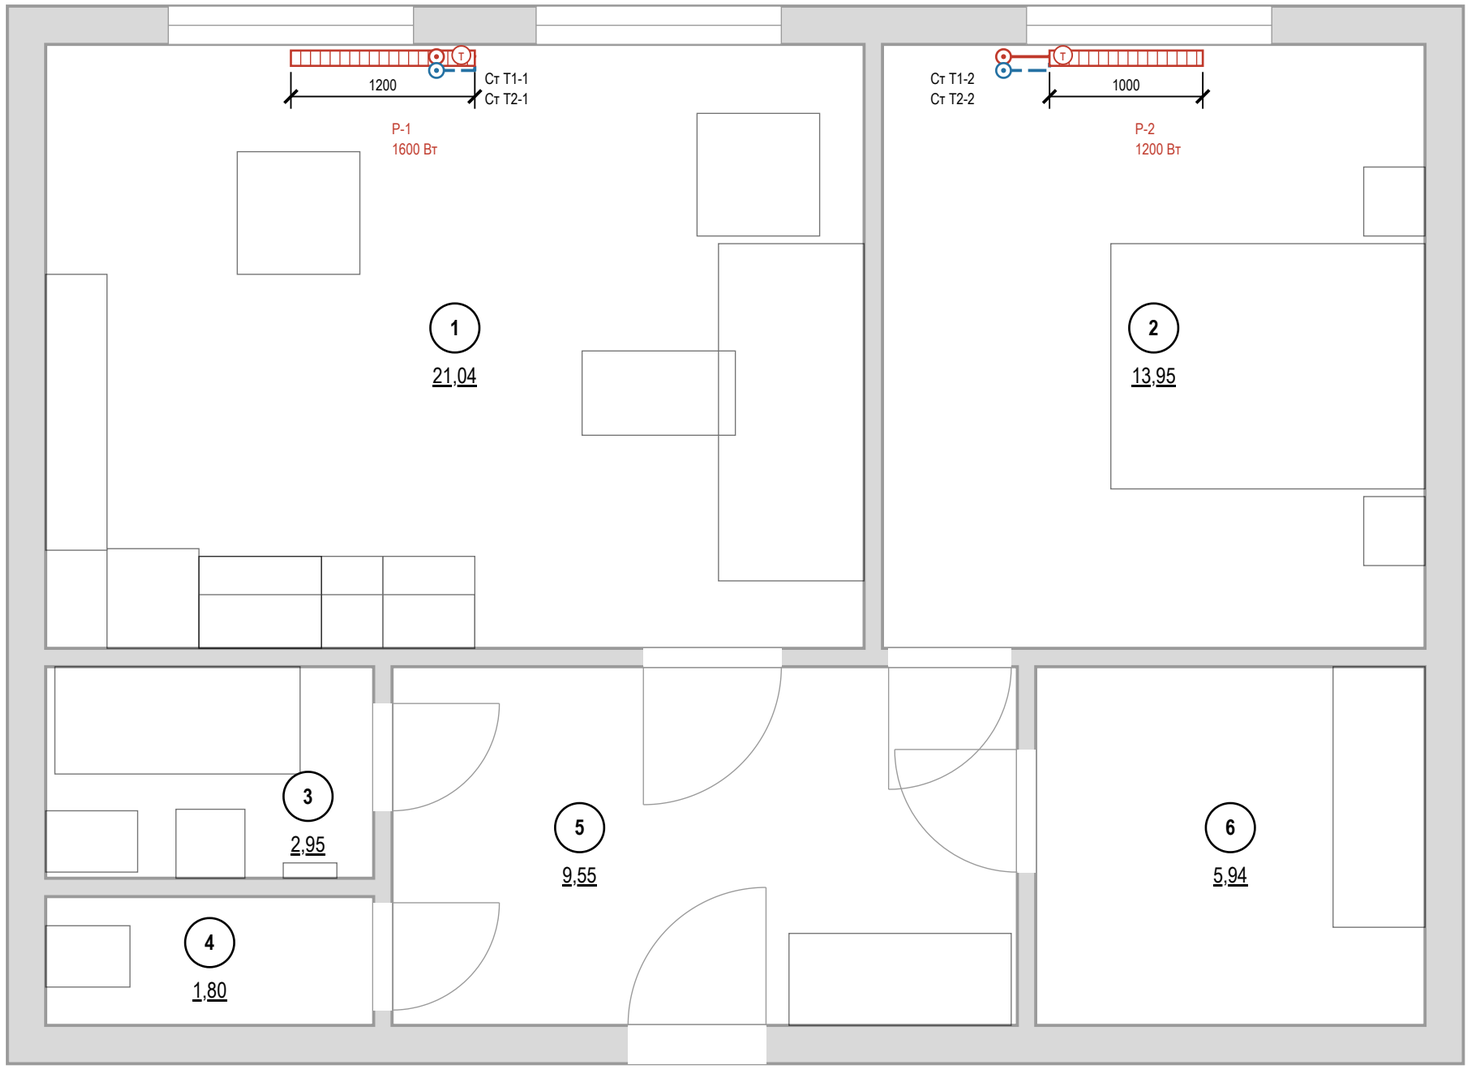

Условные обозначения

- 1 — номер помещения, площадь м²
- радиатор отопления (марка РО-N, длина по плану)
- Т — клапан с термоголовкой на подаче
- стояк отопления, подающий (Ст Т1-N)
- стояк отопления, обратный (Ст Т2-N)
- Т1 — отопление, подающий трубопровод
- Т2 — отопление, обратный трубопровод

Ведомость радиаторов

Марка	Помещение	Тип	Д×В×Г, мм	Низ / стена	Q, Вт
Р-1	1. Кухня-гостиная	панельный 22	1200×500×100	120 / 40	1600
Р-2	2. Спальня	панельный 22	1000×500×100	120 / 40	1200

Низ — от чистого пола, стена — зазор до задней панели, мм.


Привязки — до обмера
Стояки отопления в исходных данных не заданы: показаны у откосов окон, подводки — принципиально. До черновых работ — обмер стояков и паспорта приборов; лист перевыпустить по факту.

Примечания


1. Расчёт системы отопления, теплопотерь и подбор приборов — проектная организация с допуском СРО; лист даёт места и привязки.
2. Тип, длина и мощность радиаторов — по теплотехническому расчёту; лист задаёт места, зазоры и подключение.
3. Зазоры радиатора: низ не менее 100 мм от чистого пола, верх не менее 100 мм до подоконника, 30–50 мм от стены до задней панели; центр по оси окна с допуском ±20 мм.
4. Радиаторы не закрывать глухими коробами и мебелью; перенос и замена приборов в многоквартирном доме — переустройство, согласование с управляющей организацией (ЖК РФ ст. 25–26); вынос на лоджию запрещён.
5. Трубы отопления через межквартирные стены не прокладывать (СП 51.13330.2011, п. 9.19); через перекрытия и перегородки — в гильзах.
6. Привязки приборов и подводок — по паспортам приобретённых радиаторов и клапанов, до черновых работ.
7. До закрытия отделкой трубопроводы отопления испытать гидростатическим давлением с оформлением акта (СП 73.13330.2016, 7.2–7.3).

					Проект: Квартира 58 м²
	Лист	№ док.	Подпись	Дата	
Дизайнер	Кырлан А.С.			09.10.26	План отопления
					Стадия: П; Лист: 23; Листов: 60

выпуск 09.10.2026 № 7efd137e8f · стр. 23 из 60

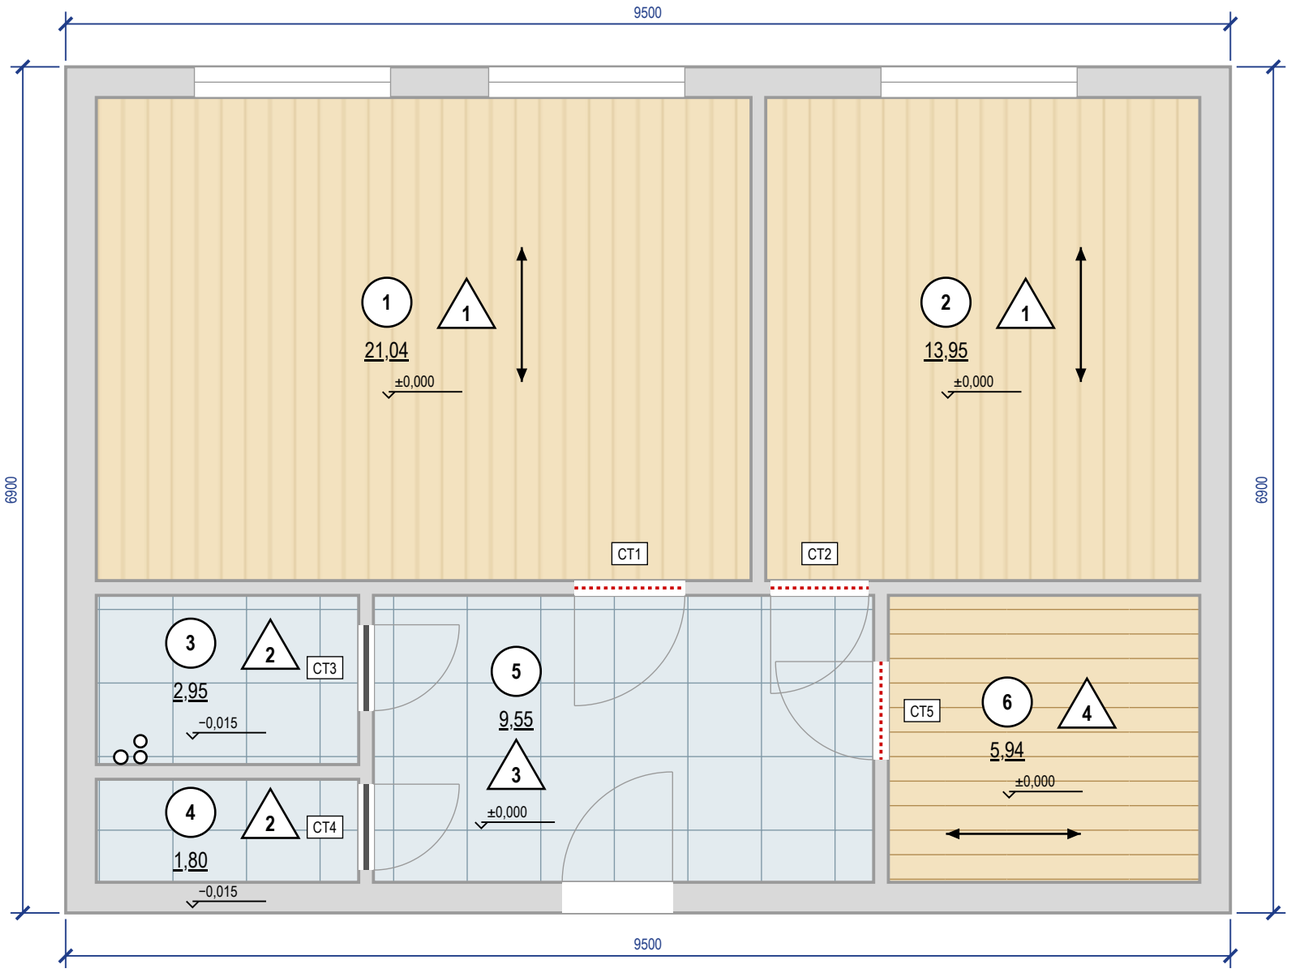

Экспликация полов

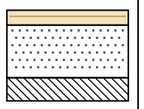Номер помещения	Тип пола	Схема пола	Данные элементов пола (наименование, толщина, основание), мм	Площадь, м²
1, 2	1		Инженерная доска, IM1861, 1380×190 мм, на клею ЧП ±0,000	34,99
3, 4	2		Керамогранит, SG651622R, 600×600 мм Гидроизоляция обмазочная, 2 слоя, с заведением на стены 200 мм ЧП −0,015	4,75
5	3		Керамогранит, SG651622R, 600×600 мм ЧП ±0,000	9,55
6	4		Инженерная доска на клею — 14 Стяжка ЦПС М200 — 50 Плита перекрытия Всего 64 мм; ЧП ±0,000, верх плиты −0,064	5,94
			Итого	**55,23**

Спецификация плинтусов

Наименование	Помещения	Длина, м (с запасом)
SX184, h = 110 мм, крепление к стене, окраска в цвет NCS S 0300-N	1, 2, 5, 6	54

Отметки по высоте

±0,000 чистый пол пом. 1, 2, 5, 6; отсчёт высот
−0,015 чистый пол пом. 3, 4, ниже на 15 мм
−0,064 верх плиты — расчёт, не замер (задание на обмер)
сущ. пол снимается до плиты; не замерен (задание на обмер)

Примечания

1. За отметку ±0,000 принят чистый пол, не существующий (блок отметок). Площади — по чистым размерам помещений, м²; размеры — в мм.
2. Стык разнотипных покрытий — по оси дверного полотна (под полотном в закрытом положении); решение стыка — по ведомости стыков.
3. Пол санузлов ниже смежных помещений на 15 мм за счёт меньшей толщины стяжки (верх плиты общий — по экспликации полов); гидроизоляция по стяжке с заведением на стены не менее 200 мм (СП 29.13330.2011, п. 7.2), до облицовки — тест проливом и акт скрытых работ.
4. Выпуски канализации с уклоном и трассы водоснабжения — в слое засыпки под стяжкой (по экспликации полов); отметки, уклоны и прочистки — по листу разводки ВК 13.
5. Звукоизоляционный слой под стяжкой проектом не предусмотрен (стяжка по плите): приведённый уровень ударного шума перекрытия с полом Lnw не более 60 дБ (СП 51.13330.2011, табл. 2) подтвердить по данным дома; при превышении — плавающая стяжка по звукоизоляции с демпферной лентой по контуру и у стояков, пирог пересчитать.
6. Штучные покрытия (инженерная доска): направление — по стрелке; влажность основания по СМ не более 2,0 % (по ТУ изготовителя).
7. Ровность основания — просвет под 2-метровой рейкой не более 2 мм: пом. 1, 2, 6 (инженерная доска), пом. 3, 4, 5 (керамогранит); проверить до укладки покрытия (СП 71.13330.2017, табл. 8.5).
8. Сетка на плитке — условная, в размер формата; точка старта и раскладка — по листу раскладки плитки.
9. Пироги полов — по экспликации полов: слои сверху вниз, толщины в мм; гидроизоляция мокрых зон — в пироге и в ведомости отделки; схема пола — без масштаба.

					Проект: Квартира 58 м²
	Лист	№ док.	Подпись	Дата	План покрытий пола
Дизайнер	Кырлан А.С.			09.10.26	

Стадия	Лист	Листов
П	24	60

выпуск 09.10.2026 № 7efd137e8f · стр. 24 из 60

Правка к этому листу

Ведомость плитки

Помещение, поверхность	Плитка, код	Формат	Шов	S, м²	Целых	Подр.	С запасом
Ванная, пол	SG651622R	600×600	2	2,95	2	10	14
Санузел, пол	SG651622R	600×600	2	1,80	0	8	9
Прихожая, пол	SG651622R	600×600	2	9,55	10	18	31
Итого 600×600				**14,30**	**12**	**36**	**54**

Ведомость материалов

Материал	Класс, код	Норма расхода	Кол-во
Затирка	класс не задан	(a+b)/ab·шов·t·1,6	1,5 кг
Клей	C2 S1	1,5 кг/м²·мм, слой 5	37 кг (2 меш.)
Клей	C2	1,5 кг/м²·мм, слой 5	78 кг (4 меш.)
Демпф. лента	по периметру пола из плитки		21,2 м

Условные обозначения

- плитка целая; тонкая линия — шов
- плитка с подрезкой (размер — на цепочке)
- ось старта; стрелки — направление укладки
- сантехприбор: габарит, высота по практике
- отметка чистого пола на полке выноски, м
- (А) обозначение стены А–Г (как на развёртках)

Примечания


1. Плитка пола мокрых помещений не задана — планы полов санузлов не выполнены; на листе — ведомость плитки остальных помещений.
2. Толщины облицовки стен не заданы: раскладка от черновых размеров, до укладки пересчитать от чистовых.
3. Раскладка пола «Ванная» и пола «Санузел» и пола «Прихожая» — на листе «Раскладка плитки. Ванная. Санузел. Прихожая».
4. Калибр партии не задан — до укладки замерить (рабочий размер W, ГОСТ 13996-2019) и пересчитать подрезки.
5. Количество: целые по раскладке + по одной на подрезку, запас 10 %; один артикул — одна партия и тон. Исключены поддон, короб, проёмы и места за коробом; S — по чистым граням, как в ведомости отделки.
6. Клей C2 S1; C2 (ГОСТ Р 56387-2018), затирка класс не задан; расход — по ТУ выбранной марки.

					Проект: Квартира 58 м²		
	Лист	№ док.	Подпись	Дата	Раскладка плитки. Планы полов	Стадия	Лист	Листов
Дизайнер	Кырлан А.С.			09.10.26		П	25	60


выпуск 09.10.2026 № 7efd137e8f · стр. 25 из 60

Правка к этому листу

Фрагмент 1. Ванная (пом. 3). Пол 600×600, шов 2 мм, М 1:25

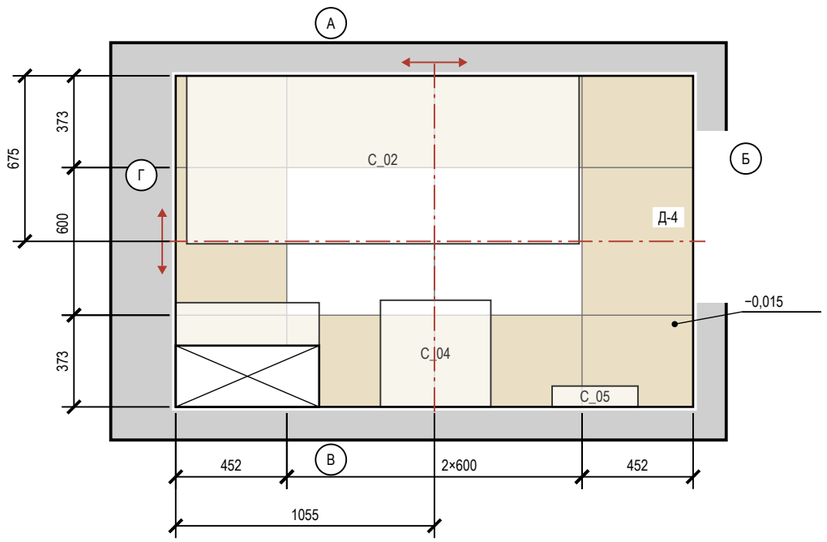

Фрагмент 2. Санузел (пом. 4). Пол 600×600, шов 2 мм, М 1:25

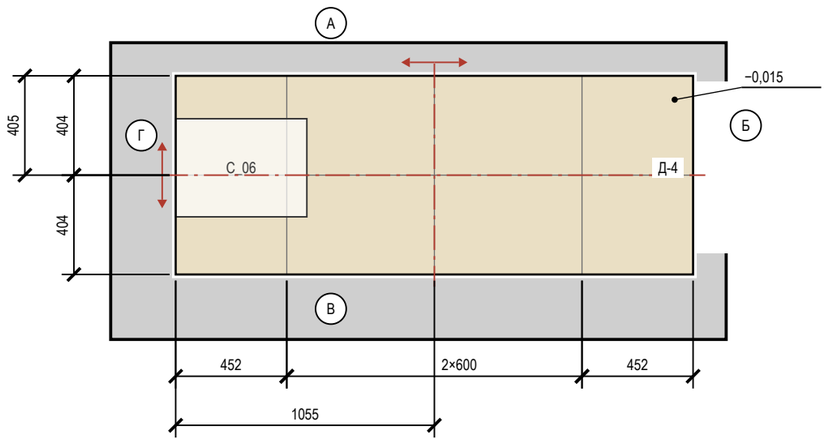

Условные обозначения

- плитка целая; тонкая линия — шов
- плитка с подрезкой (размер — на цепочке)
- ось старта; стрелки — направление укладки
- отметка чистого пола на полке выноски, м
- А — обозначение стены А–Г (как на развёртках)


Подсчёт плитки

Поверхность	Формат	S, м²	Целых	Подр.	С запасом
Ванная, пол	600×600	2,95	2	10	14
Санузел, пол	600×600	1,80	0	8	9
Прихожая, пол	600×600	9,55	10	18	31

Примечания

1. Ванная: керамогранит 600×600, длинная сторона — вдоль стен Б и Г, шов 2 мм, прямая раскладка от центра. Стены окрашены: раскладка от чистового контура минус штукатурка и шпаклёвка 15 мм на сторону (принято); подрезки 452 / 373 мм, срез — под плинтус.
2. Ванная: деформационный зазор по периметру 8–10 мм под плинтусом; в проёмах — стык с соседним покрытием по оси полотна двери. Клей С2 S1, затирка класс не задан.
3. Санузел: керамогранит 600×600, длинная сторона — вдоль стен Б и Г, шов 2 мм, прямая раскладка от центра. Стены окрашены: раскладка от чистового контура минус штукатурка и шпаклёвка 15 мм на сторону (принято); подрезки 452 / 404 мм, срез — под плинтус.
4. Санузел: деформационный зазор по периметру 8–10 мм под плинтусом; в проёмах — стык с соседним покрытием по оси полотна двери. Клей С2 S1, затирка класс не задан.
5. Прихожая: керамогранит 600×600, длинная сторона — вдоль стен Б и Г, шов 2 мм, прямая раскладка от центра. Стены окрашены: раскладка от чистового контура минус штукатурка и шпаклёвка 15 мм на сторону (принято); подрезки 519 / 552 мм, срез — под плинтус.
6. Прихожая: деформационный зазор по периметру 8–10 мм под плинтусом; в проёмах — стык с соседним покрытием по оси полотна двери. Клей С2, затирка класс не задан.
7. Клей, затирка и итог по форматам — в ведомостях листа «Раскладка плитки. Планы полов».

Фрагмент 3. Прихожая (пом. 5). Пол 600×600, шов 2 мм, М 1:25

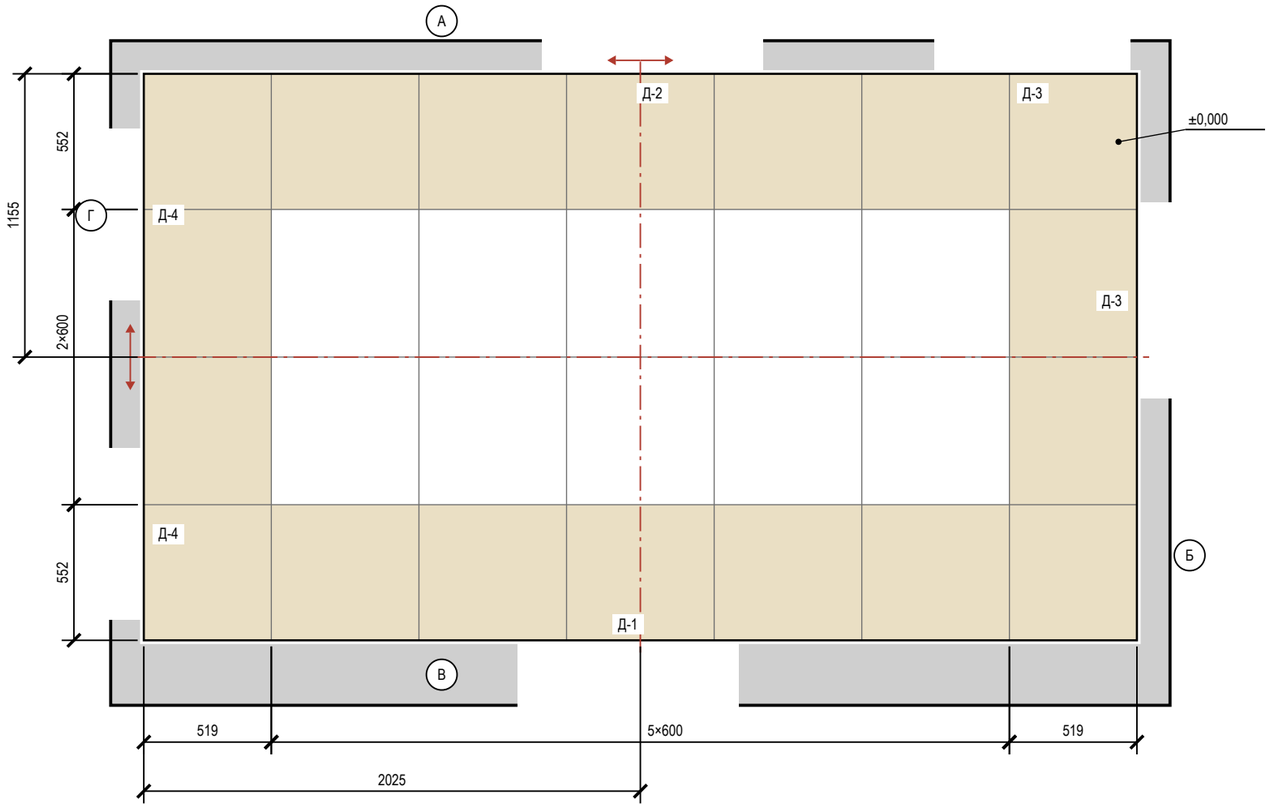

					Проект: Квартира 58 м²
	Лист	№ док.	Подпись	Дата	Раскладка плитки. Ванная. Санузел. Прихожая
Дизайнер	Кырлан А.С.			09.10.26	

Стадия	Лист	Листов
П	26	60

выпуск 09.10.2026 № 7efd137e8f · стр. 26 из 60

Правка к этому листу



					Проект: Квартира 58 м²	
	Лист	№ док.	Подпись	Дата	Визуализация кухни-гостиной	Стадия / Лист / Листов
Дизайнер	Кырлан А.С.			09.10.26		П / 27 / 60

выпуск 09.10.2026 № 7efd137e8f · стр. 27 из 60

Правка к этому листу



					Проект: Квартира 58 м²
	Лист	№ док.	Подпись	Дата	Визуализация кухни-гостиной
Дизайнер	Кырлан А.С.			09.10.26	

Стадия	Лист	Листов
П	28	60

выпуск 09.10.2026 № 7efd137e8f · стр. 28 из 60

Правка к этому листу



					Проект: Квартира 58 м²	
	Лист	№ док.	Подпись	Дата	Визуализация кухни-гостиной	Стадия / Лист / Листов
Дизайнер	Кырлан А.С.			09.10.26		П / 29 / 60

выпуск 09.10.2026 СР 7efd137e8f · стр. 29 из 60

Правка к этому листу

Развёртка стены В


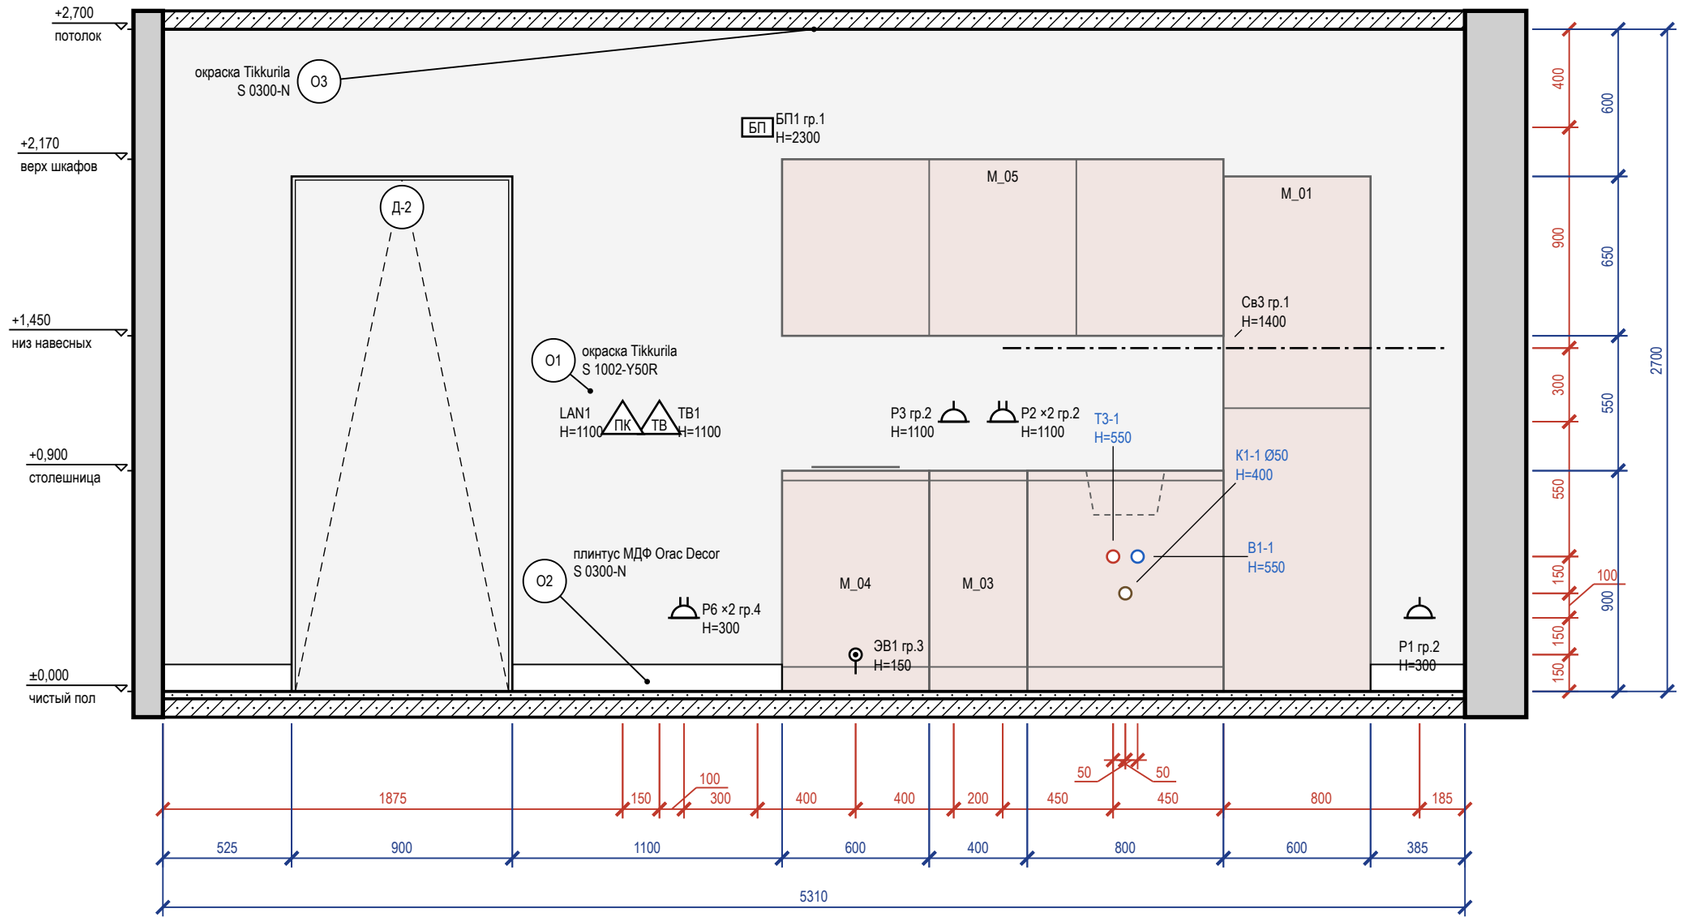


Схема развёрток (М 1:100)

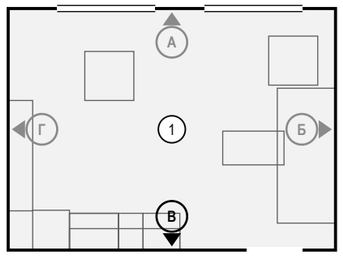

Ведомость отделки (на листе)

Марка	Поверхность	Материал, изделие	Цвет, код	Кол.
О1	стены	окраска, Tikkurila, шелковисто-матовая, подготовка Q3	NCS S 1002-Y50R	12,4 м²
О2	плинтус	плинтус МДФ, Orac Decor Luxxus, h 110 мм, SX184, шелковисто-матовая	NCS S 0300-N	2 м
О3	потолок	окраска, Tikkurila, глубокоматовая	NCS S 0300-N	21 м²

Визуализация этой стены — лист 28



Примечания

1. Размеры — в мм от чистовых поверхностей стен; условные обозначения и общие указания — лист 2.
2. Двери скрытого монтажа — полотно в плоскости стены, отделка стены по полотну, плинтус прерывается у короба (узел — на листе узлов).
3. Выводы кухонной техники — по утверждённому проекту кухни: привязки выводов даются от осей модулей гарнитура.

					Проект: Квартира 58 м²
	Лист	№ док.	Подпись	Дата	Развёртка стены В. Кухня-гостиная (пом. 1), кухонный фронт
Дизайнер	Кырлан А.С.			09.10.26	

Стадия	Лист	Листов
П	30	60

выпуск 09.10.2026 № 7efd137e8f · стр. 30 из 60

Правка к этому листу

Развёртка стены А


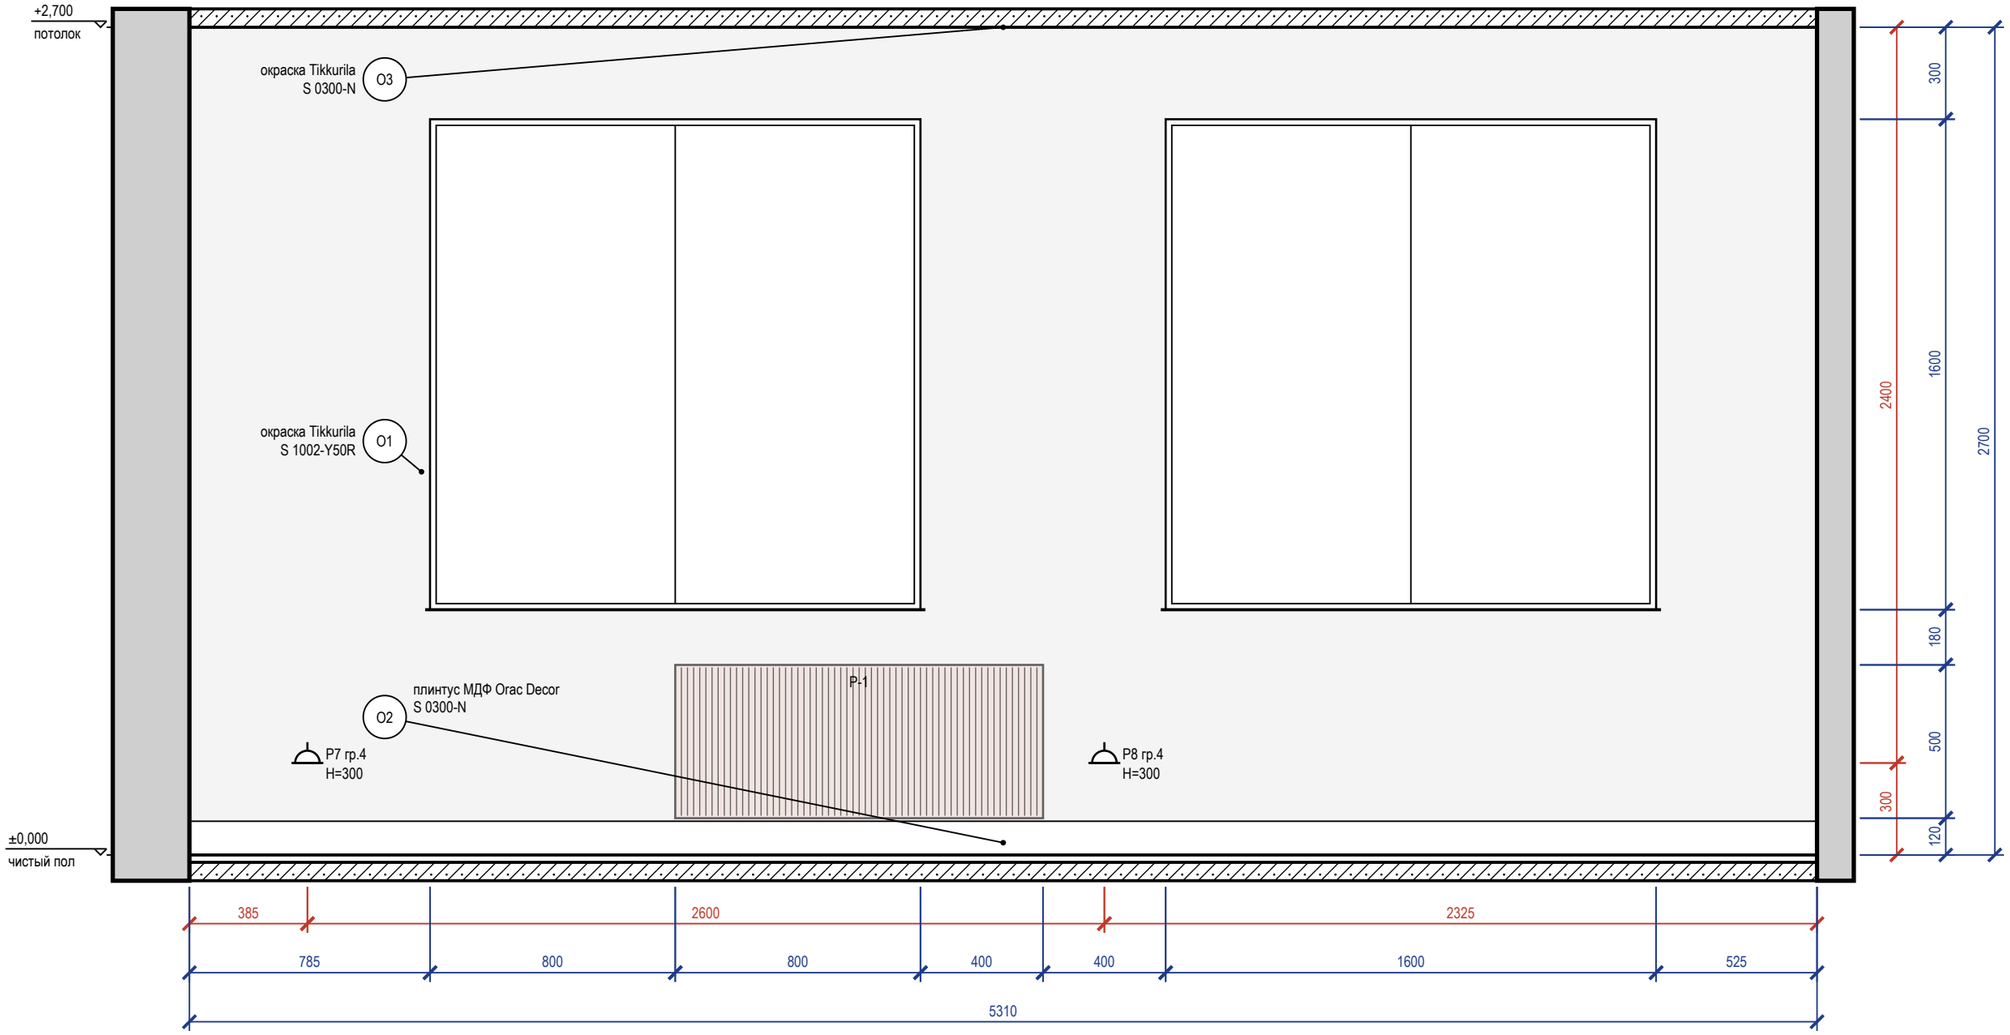


Схема развёрток (М 1:100)

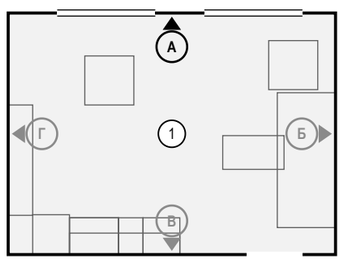

Ведомость отделки (на листе)

Марка	Поверхность	Материал, изделие	Цвет, код	Кол.
О1	стены	окраска, Tikkurila, шелковисто-матовая, подготовка Q3	NCS S 1002-Y50R	9,2 м²
О2	плинтус	плинтус МДФ, Orac Decor Luxxus, h 110 мм, SX184, шелковисто-матовая	NCS S 0300-N	5,3 м
О3	потолок	окраска, Tikkurila, глубокоматовая	NCS S 0300-N	21 м²

Примечания

1. Размеры — в мм от чистовых поверхностей стен; условные обозначения и общие указания — лист 2.

					Проект: Квартира 58 м²
	Лист	№ док.	Подпись	Дата	
Дизайнер	Кырлан А.С.			09.10.26	Развёртка стены А. Кухня-гостиная (пом. 1)

Стадия	Лист	Листов
П	31	60

выпуск 09.10.2026 № 7efd137e8f · стр. 31 из 60

Правка к этому листу

Развёртка стены Б


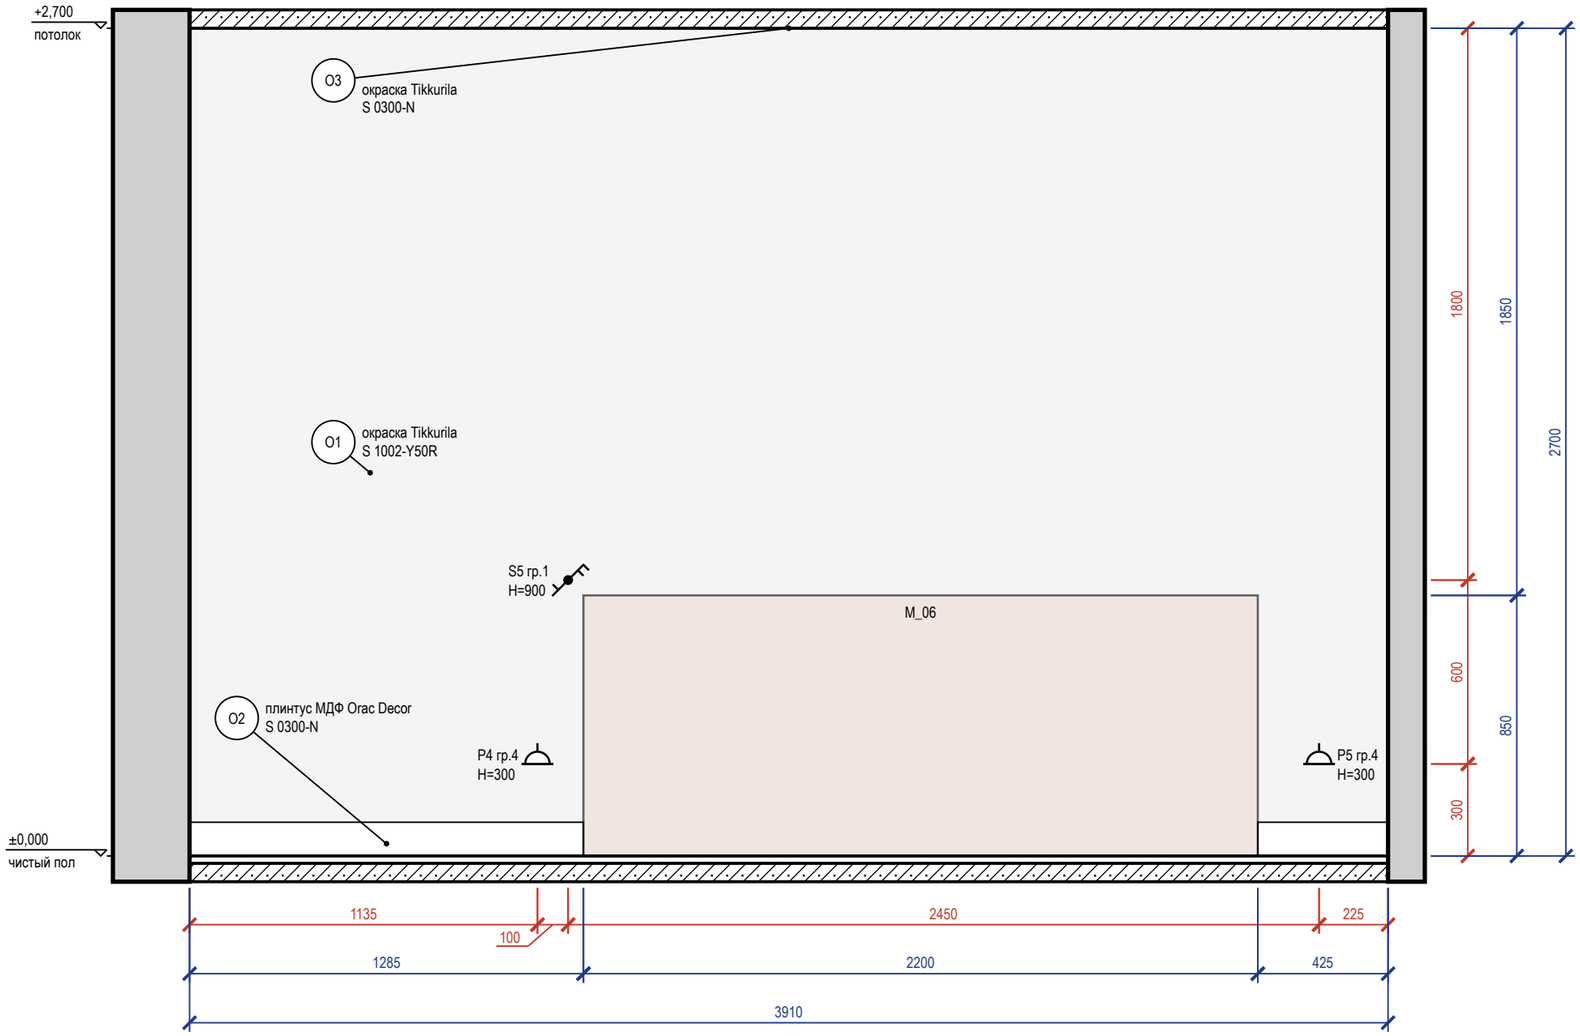


Схема развёрток (М 1:100)

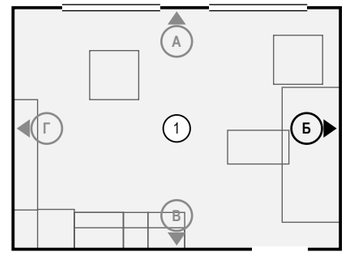

Ведомость отделки (на листе)

Марка	Поверхность	Материал, изделие	Цвет, код	Кол.
О1	стены	окраска, Tikkurila, шелковисто-матовая, подготовка Q3	NCS S 1002-Y50R	10,6 м²
О2	плинтус	плинтус МДФ, Orac Decor Luxxus, h 110 мм, SX184, шелковисто-матовая	NCS S 0300-N	1,7 м
О3	потолок	окраска, Tikkurila, глубокоматовая	NCS S 0300-N	21 м²

Визуализация этой стены — лист 27



Примечания

1. Размеры — в мм от чистовых поверхностей стен; условные обозначения и общие указания — лист 2.

					Проект: Квартира 58 м²
	Лист	№ док.	Подпись	Дата	Развёртка стены Б. Кухня-гостиная (пом. 1)
Дизайнер	Кырлан А.С.			09.10.26	

Стадия	Лист	Листов
П	32	60

Правка к этому листу

Развёртка стены Г


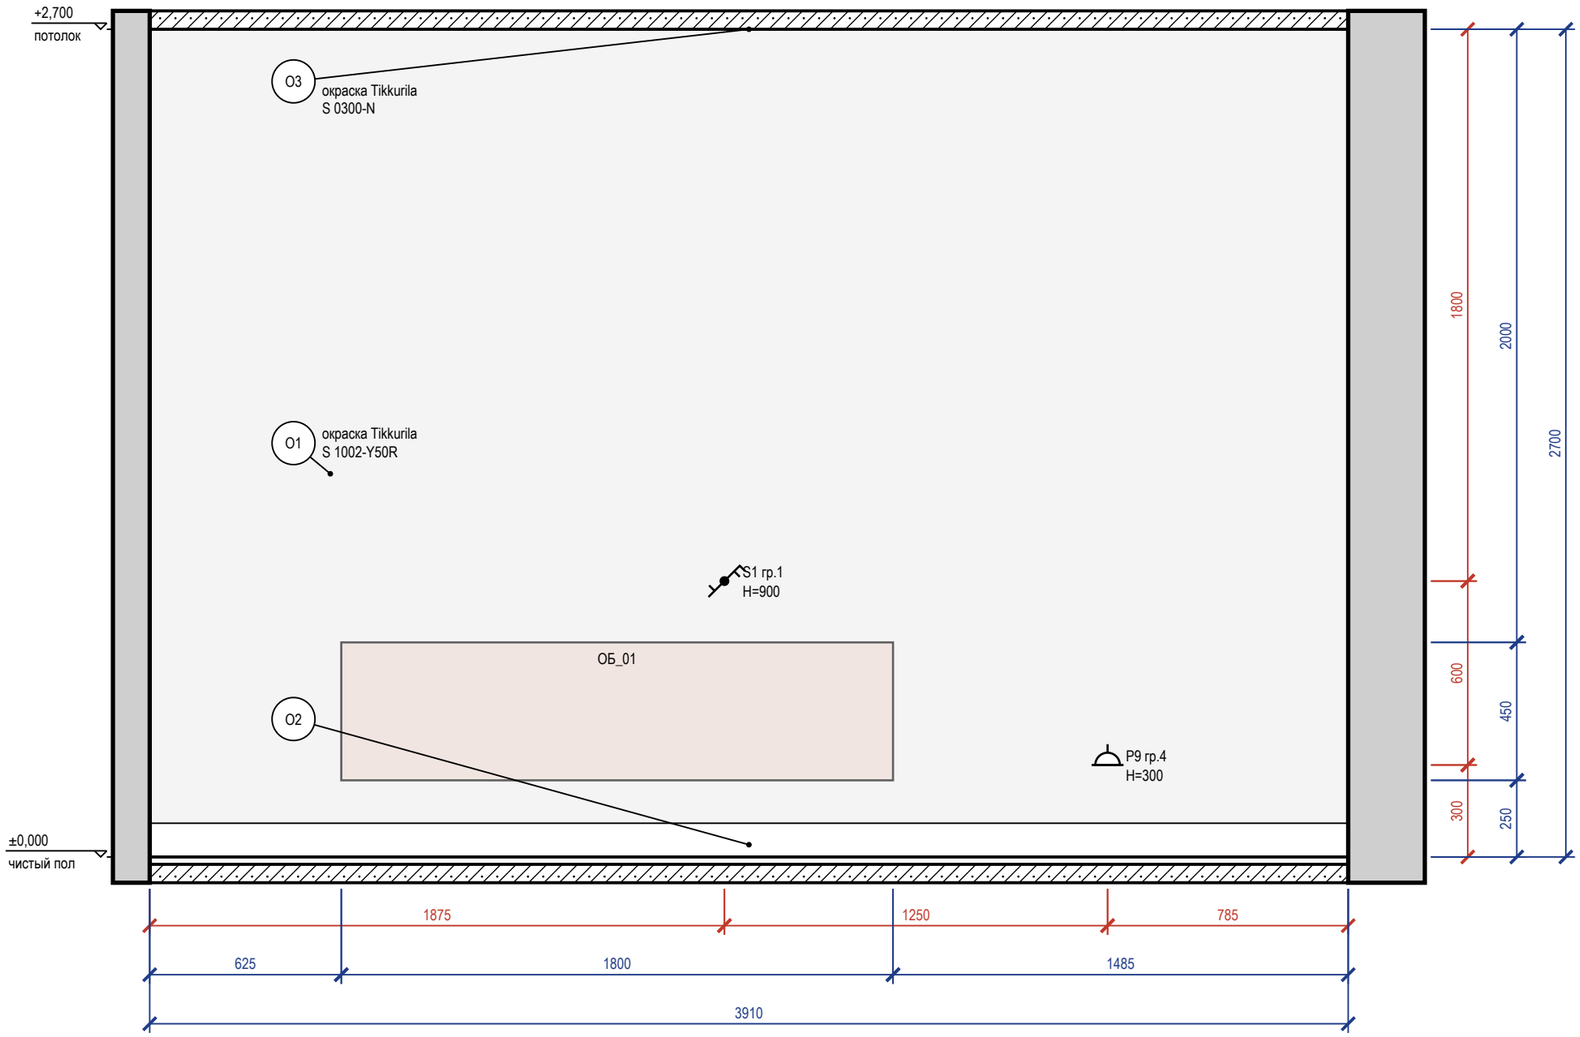


Схема развёрток (М 1:100)

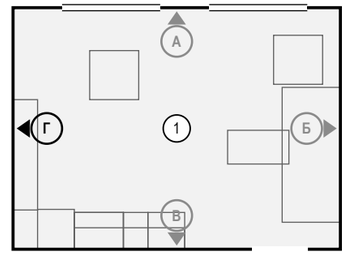

Ведомость отделки (на листе)

Марка	Поверхность	Материал, изделие	Цвет, код	Кол.
О1	стены	окраска, Tikkurila, шелковисто-матовая, подготовка Q3	NCS S 1002-Y50R	10,6 м²
О2	плинтус	плинтус МДФ, Orac Decor Luxxus, h 110 мм, SX184, шелковисто-матовая	NCS S 0300-N	3,9 м
О3	потолок	окраска, Tikkurila, глубокоматовая	NCS S 0300-N	21 м²

Визуализация этой стены — лист 29



Примечания

1. Размеры — в мм от чистовых поверхностей стен; условные обозначения и общие указания — лист 2.

					Проект: Квартира 58 м²
	Лист	№ док.	Подпись	Дата	Развёртка стены Г. Кухня-гостиная (пом. 1)
Дизайнер	Кырлан А.С.			09.10.26	

Стадия	Лист	Листов
П	33	60

Правка к этому листу



					Проект: Квартира 58 м²
	Лист	№ док.	Подпись	Дата	
Дизайнер	Кырлан А.С.			09.10.26	Визуализация спальни

Стадия	Лист	Листов
П	34	60

выпуск 09.10.2026 № 7efd137e8f · стр. 34 из 60

Правка к этому листу



					Проект: Квартира 58 м²	
	Лист	№ док.	Подпись	Дата	Визуализация спальни	Стадия / Лист / Листов
Дизайнер	Кырлан А.С.			09.10.26		П / 35 / 60

выпуск 09.10.2026 № 7efd137e8f · стр. 35 из 60

Правка к этому листу

Развёртка стены А


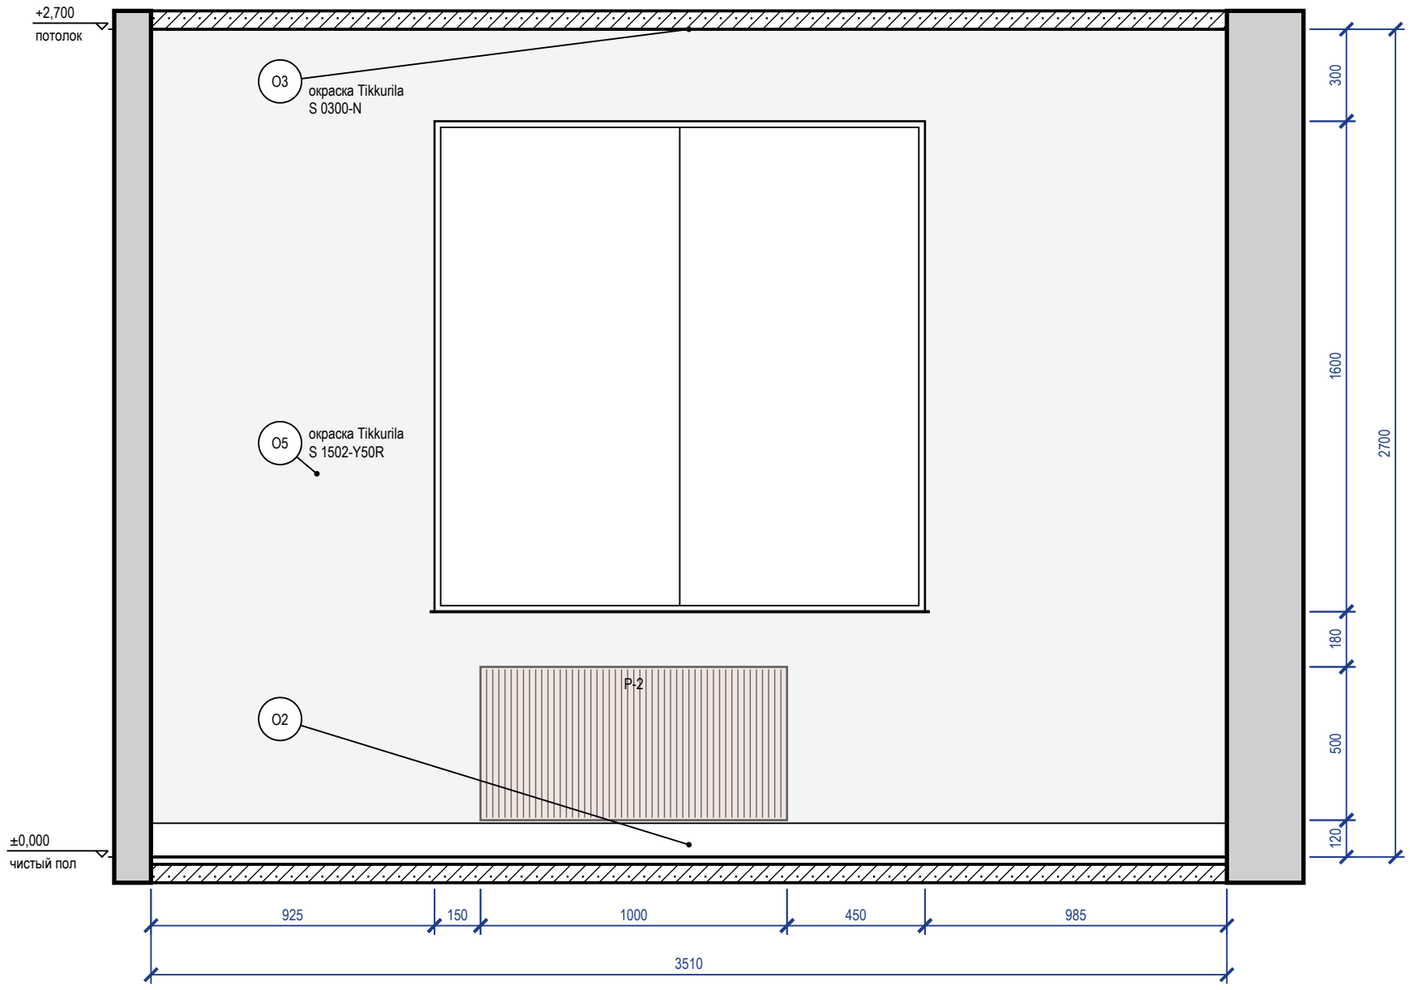


Схема развёрток (М 1:100)

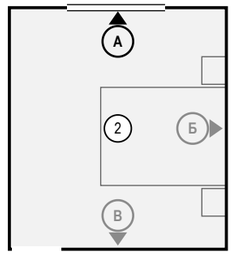

Ведомость отделки (на листе)

Марка	Поверхность	Материал, изделие	Цвет, код	Кол.
О2	плинтус	плинтус МДФ, Orac Decor Luxxus, h 110 мм, SX184, шелковисто-матовая	NCS S 0300-N	3,5 м
О3	потолок	окраска, Tikkurila, глубокоматовая	NCS S 0300-N	13,9 м²
О5	стены	окраска, Tikkurila, глубокоматовая, подготовка Q3	NCS S 1502-Y50R	6,9 м²

Визуализация этой стены — лист 34



Примечания

1. Размеры — в мм от чистовых поверхностей стен; условные обозначения и общие указания — лист 2.

					Проект: Квартира 58 м²
	Лист	№ док.	Подпись	Дата	Развёртка стены А. Спальня (пом. 2)
Дизайнер	Кырлан А.С.			09.10.26	

Стадия	Лист	Листов
П	36	60

выпуск 09.10.2026 № 7efd137e8f · стр. 36 из 60

Правка к этому листу

Развёртка стены Б


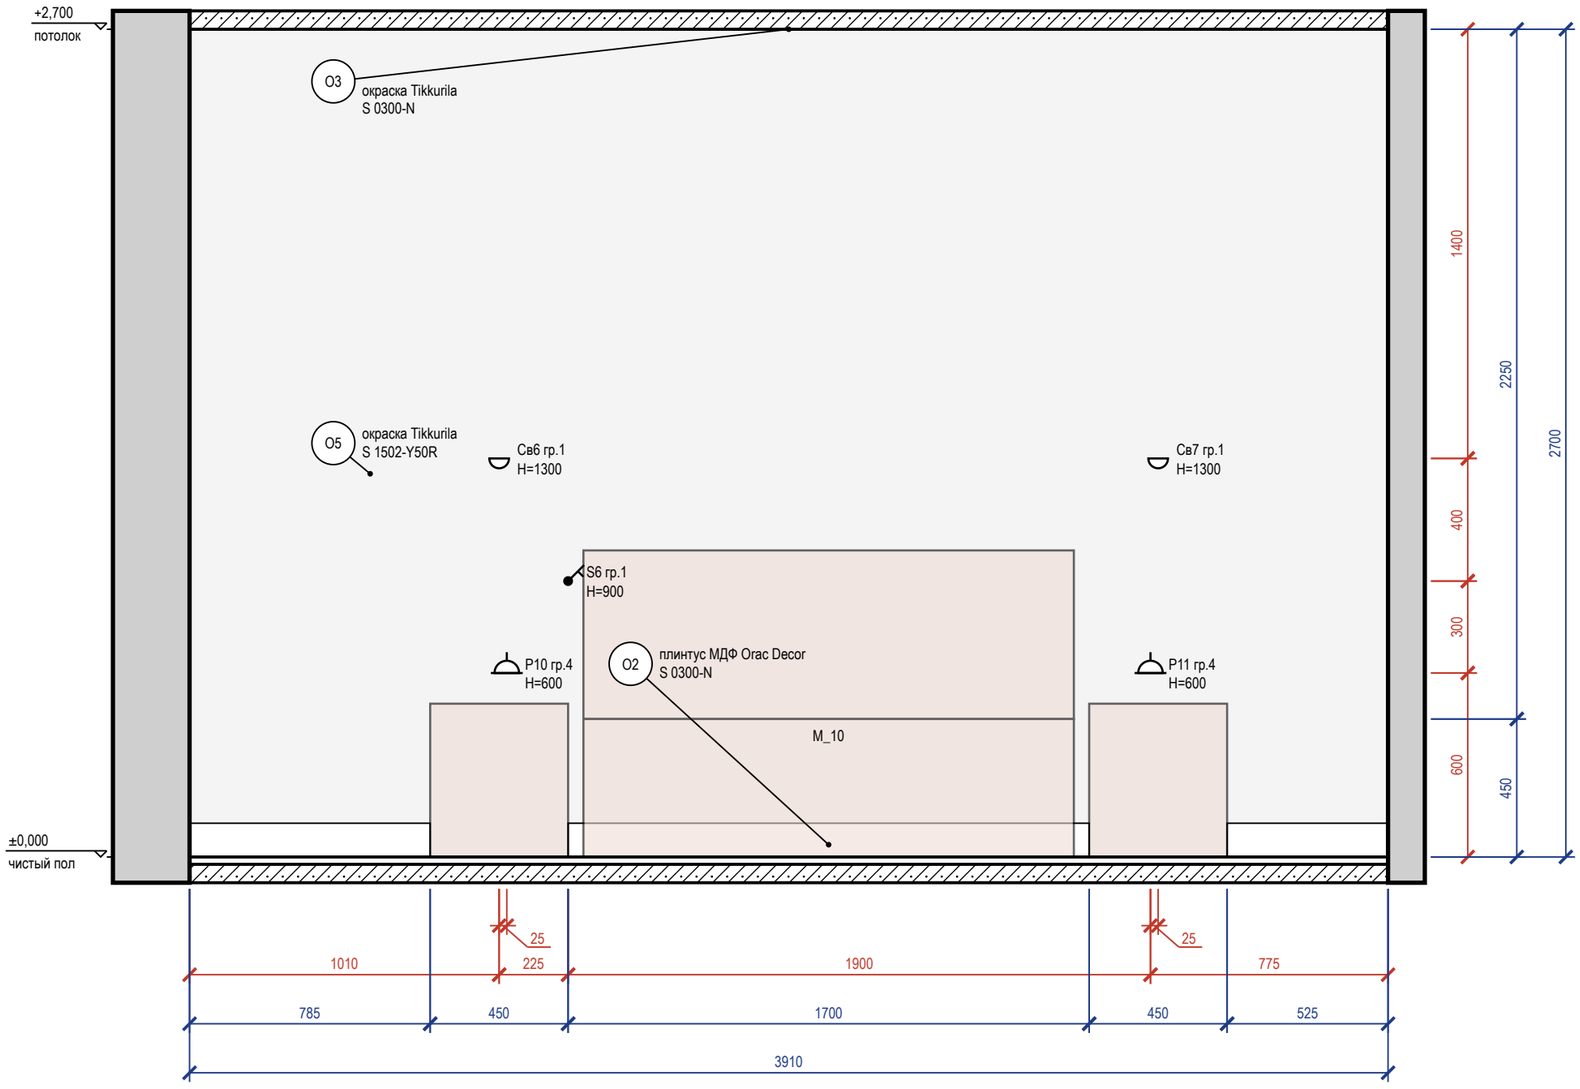


Схема развёрток (М 1:100)

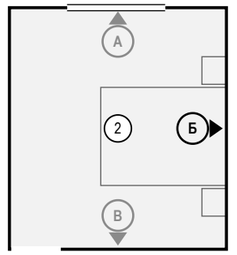

Ведомость отделки (на листе)

Марка	Поверхность	Материал, изделие	Цвет, код	Кол.
О2	плинтус	плинтус МДФ, Orac Decor Luxxus, h 110 мм, SX184, шелковисто-матовая	NCS S 0300-N	3 м
О3	потолок	окраска, Tikkurila, глубокоматовая	NCS S 0300-N	13,9 м²
О5	стены	окраска, Tikkurila, глубокоматовая, подготовка Q3	NCS S 1502-Y50R	10,6 м²

Визуализация этой стены — лист 35



Примечания

1. Размеры — в мм от чистовых поверхностей стен; условные обозначения и общие указания — лист 2.

					Проект: Квартира 58 м²	
	Лист	№ док.	Подпись	Дата	Развёртка стены Б. Спальня (пом. 2)	Стадия / Лист / Листов
Дизайнер	Кырлан А.С.			09.10.26		П / 37 / 60

выпуск 09.10.2026 № 7efd137e8f · стр. 37 из 60

Правка к этому листу

Развёртка стены В


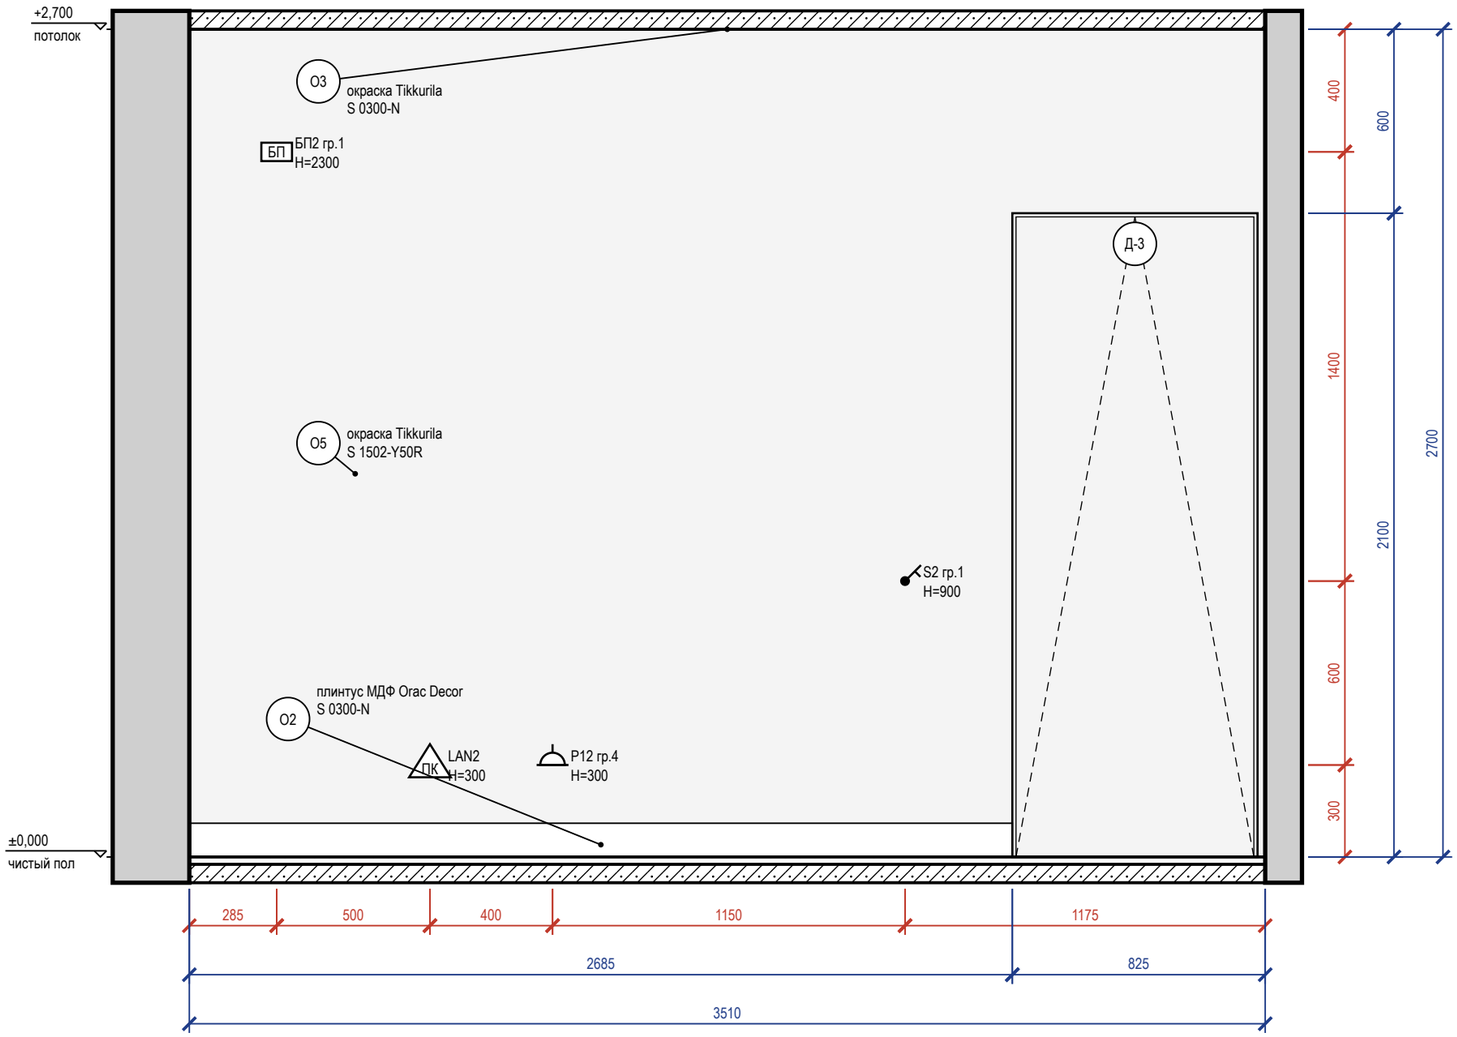


Схема развёрток (М 1:100)

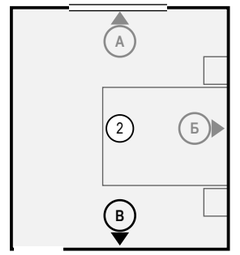


Ведомость отделки (на листе)

Марка	Поверхность	Материал, изделие	Цвет, код	Кол.
О2	плинтус	плинтус МДФ, Orac Decor Luxxus, h 110 мм, SX184, шелковисто-матовая	NCS S 0300-N	2,7 м
О3	потолок	окраска, Tikkurila, глубокоматовая	NCS S 0300-N	13,9 м²
О5	стены	окраска, Tikkurila, глубокоматовая, подготовка Q3	NCS S 1502-Y50R	7,8 м²

5 **Плинтус МДФ 110×16 мм у окрашенной стены (М 1:10)**

Узел 5 — лист С3

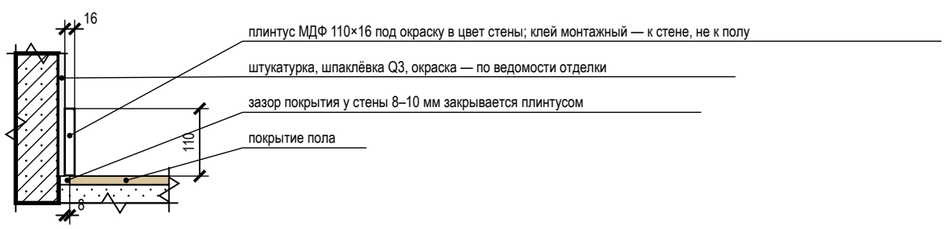

Примечания

1. Размеры — в мм от чистовых поверхностей стен; условные обозначения и общие указания — лист 2.
2. Двери скрытого монтажа — полотно в плоскости стены, отделка стены по полотну, плинтус прерывается у короба (узел — на листе узлов).

	Лист	№ док.	Подпись	Дата
Дизайнер	Кырлан А.С.			09.10.26

Проект: Квартира 58 м²

Развёртка стены В. Спальня (пом. 2)

Стадия	Лист	Листов
П	38	60

выпуск 09.10.2026 № 7efd137e8f · стр. 38 из 60

Правка к этому листу



					Проект: Квартира 58 м²	
	Лист	№ док.	Подпись	Дата	Визуализация ванной	Стадия / Лист / Листов
Дизайнер	Кырлан А.С.			09.10.26		П / 39 / 60

выпуск 09.10.2026 · 7efd137e8f · стр. 39 из 60

Правка к этому листу




					Проект: Квартира 58 м²
	Лист	№ док.	Подпись	Дата	
Дизайнер	Кырлан А.С.			09.10.26	Визуализация ванной

Стадия	Лист	Листов
П	40	60

выпуск 09.10.2026 № 7efd137e8f · стр. 40 из 60

Правка к этому листу

Развёртка стены А

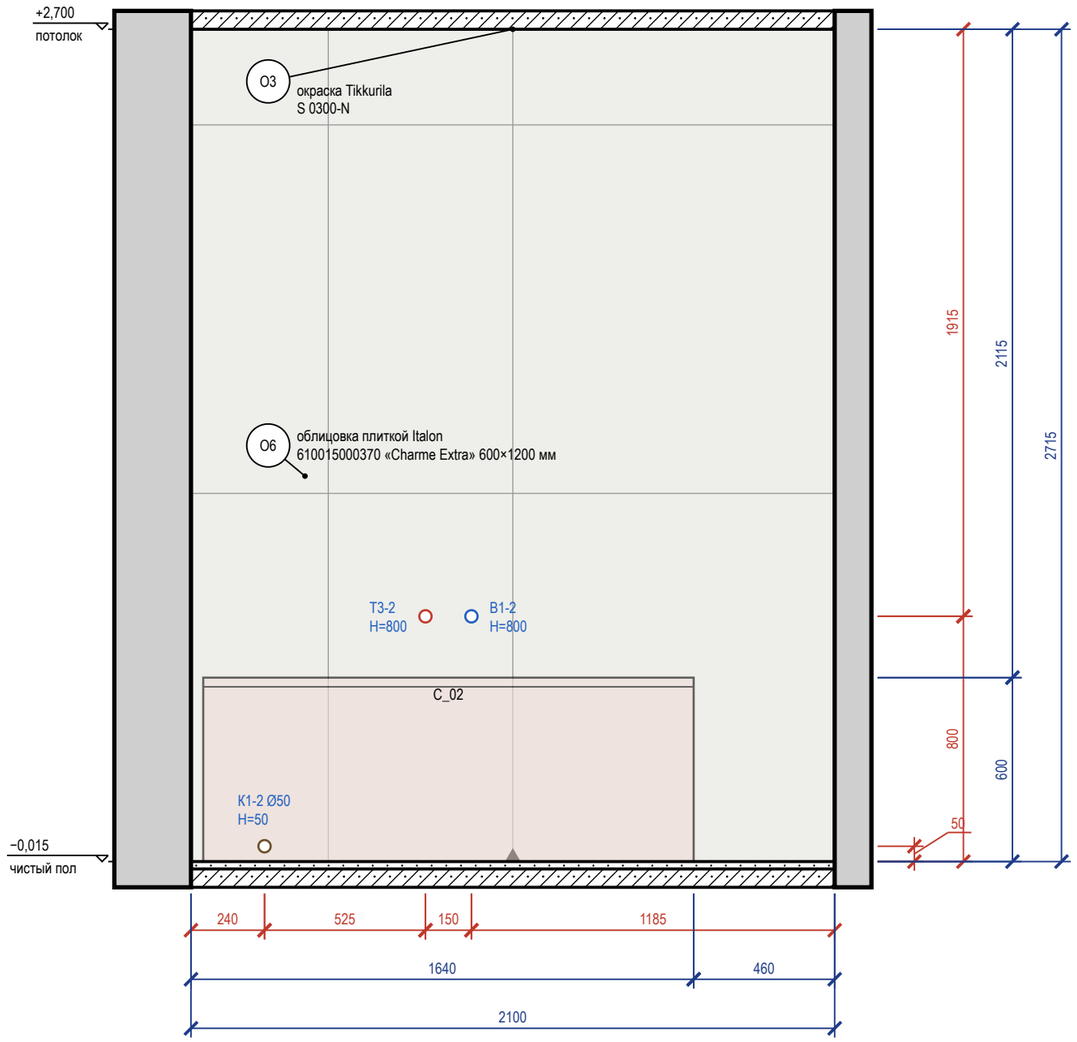

Развёртка стены Б


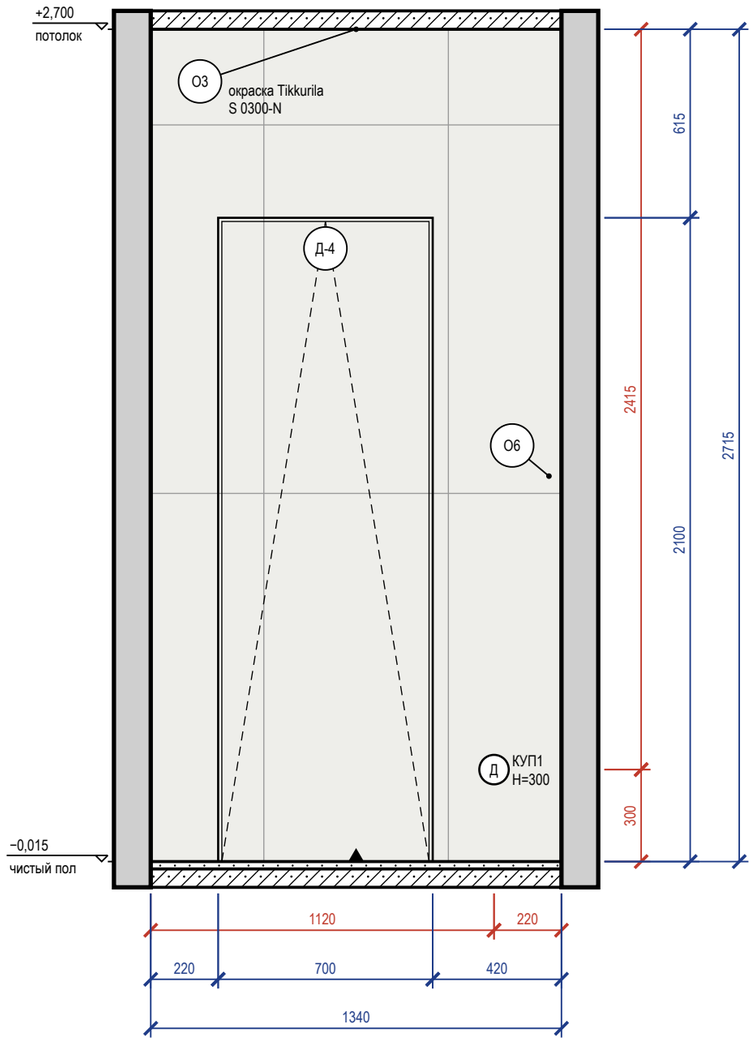


Схема развёрток (М 1:100)

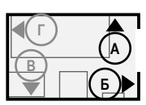

Ведомость отделки (на листе)

Марка	Поверхность	Материал, изделие	Цвет, код	Кол.
О3	потолок	окраска, Tikkurila, глубокоматовая	NCS S 0300-N	3 м²
О6	стены	облицовка плиткой, Italon Charme Extra, 600×1200 мм, 610015000370	Italon 610015000370 «Charme Extra»	7,9 м²

Визуализация этой стены — лист 39



Примечания


1. Размеры — в мм от чистовых поверхностей стен; условные обозначения и общие указания — лист 2.
2. Облицовка — по сетке швов, раскладка от оси стены (треугольник у пола); подрезки — по листу раскладки плитки.
3. Гидроизоляция в 2 слоя, заход на стены 200 мм — до облицовки, с актом скрытых работ и тестом проливом (узел — на листе узлов).
4. Двери скрытого монтажа — полотно в плоскости стены, отделка стены по полотну, плинтус прерывается у короба (узел — на листе узлов).

	Лист	№ док.	Подпись	Дата	Проект: Квартира 58 м²			
Дизайнер	Кырлан А.С.			09.10.26	Развёртки стен А, Б. Ванная (пом. 3)	Стадия	Лист	Листов
						П	41	60

выпуск 09.10.2026 № 7efd137e8f · стр. 41 из 60

Правка к этому листу

Развёртка стены В

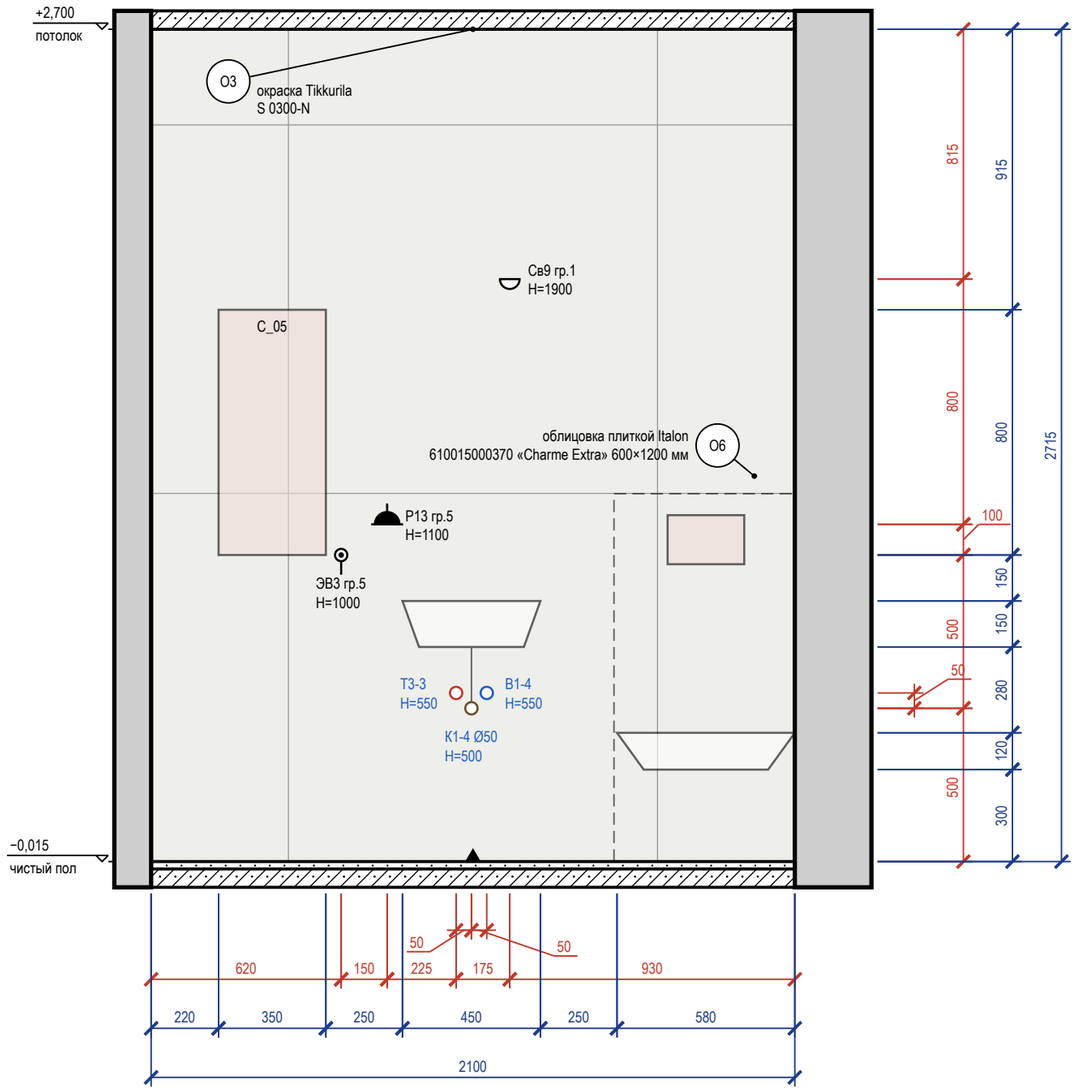

Развёртка стены Г


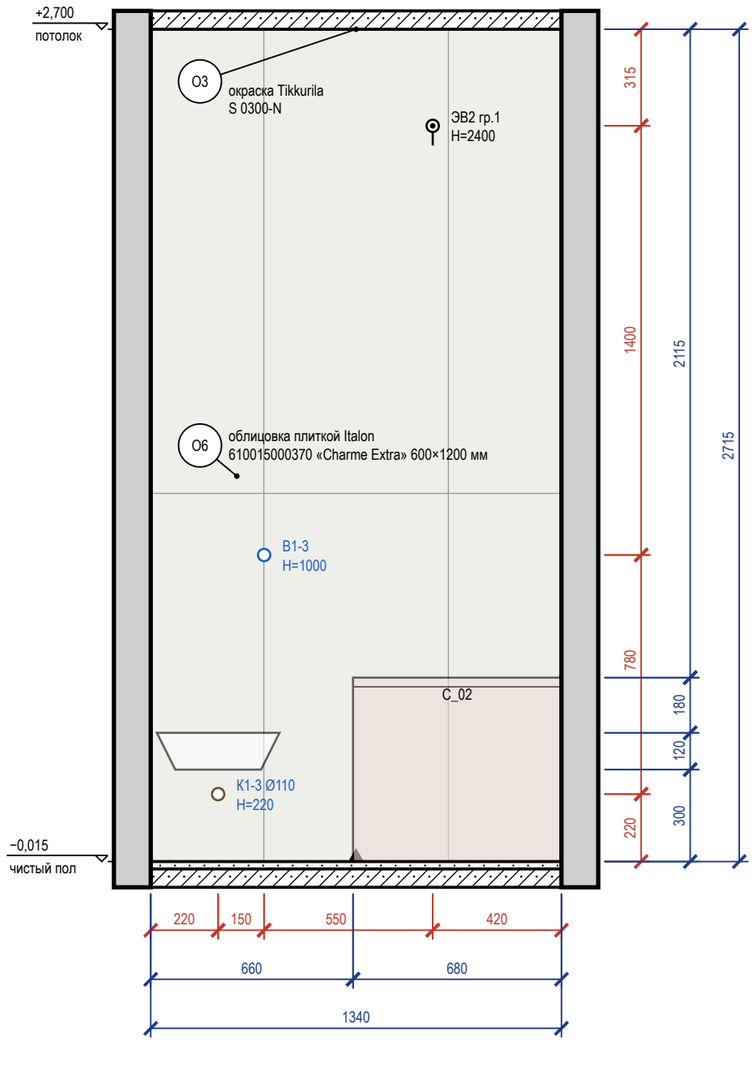



Схема развёрток (М 1:100)

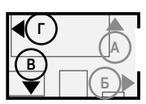

Ведомость отделки (на листе)

Марка	Поверхность	Материал, изделие	Цвет, код	Кол.
О3	потолок	окраска, Tikkurila, глубокоматовая	NCS S 0300-N	3 м²
О6	стены	облицовка плиткой, Italon Charme Extra, 600×1200 мм, 610015000370	Italon 610015000370 «Charme Extra»	9,3 м²

Визуализация этой стены — лист 40

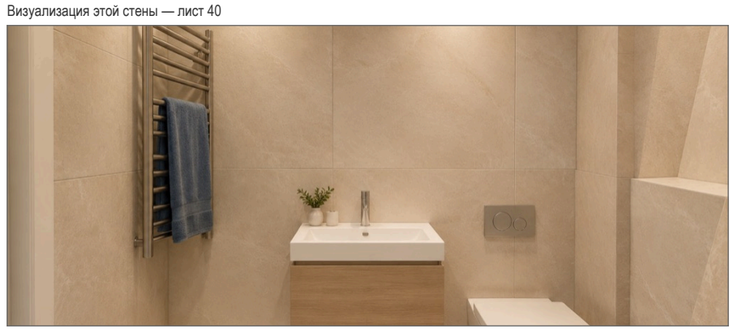

Примечания

1. Размеры — в мм от чистовых поверхностей стен; условные обозначения и общие указания — лист 2.
2. Схема мебели, приборов и декора не является технической документацией для производства мебели; габариты — по паспортам изделий.
3. Облицовка — по сетке швов, раскладка от оси стены (треугольник у пола); подрезки — по листу раскладки плитки.
4. Гидроизоляция в 2 слоя, заход на стены 200 мм — до облицовки, с актом скрытых работ и тестом проливом (узел — на листе узлов).

					Проект: Квартира 58 м²
	Лист	№ док.	Подпись	Дата	Развёртки стен В, Г. Ванная (пом. 3)
Дизайнер	Кырлан А.С.			09.10.26	

Стадия	Лист	Листов
П	42	60

выпуск 09.10.2026 № 7efd137e8f · стр. 42 из 60

Правка к этому листу




					Проект: Квартира 58 м²
	Лист	№ док.	Подпись	Дата	Визуализация санузла
Дизайнер	Кырлан А.С.			09.10.26	

Стадия	Лист	Листов
П	43	60

выпуск 09.10.2026 7efd137e8f · стр. 43 из 60

Правка к этому листу

Развёртка стены А

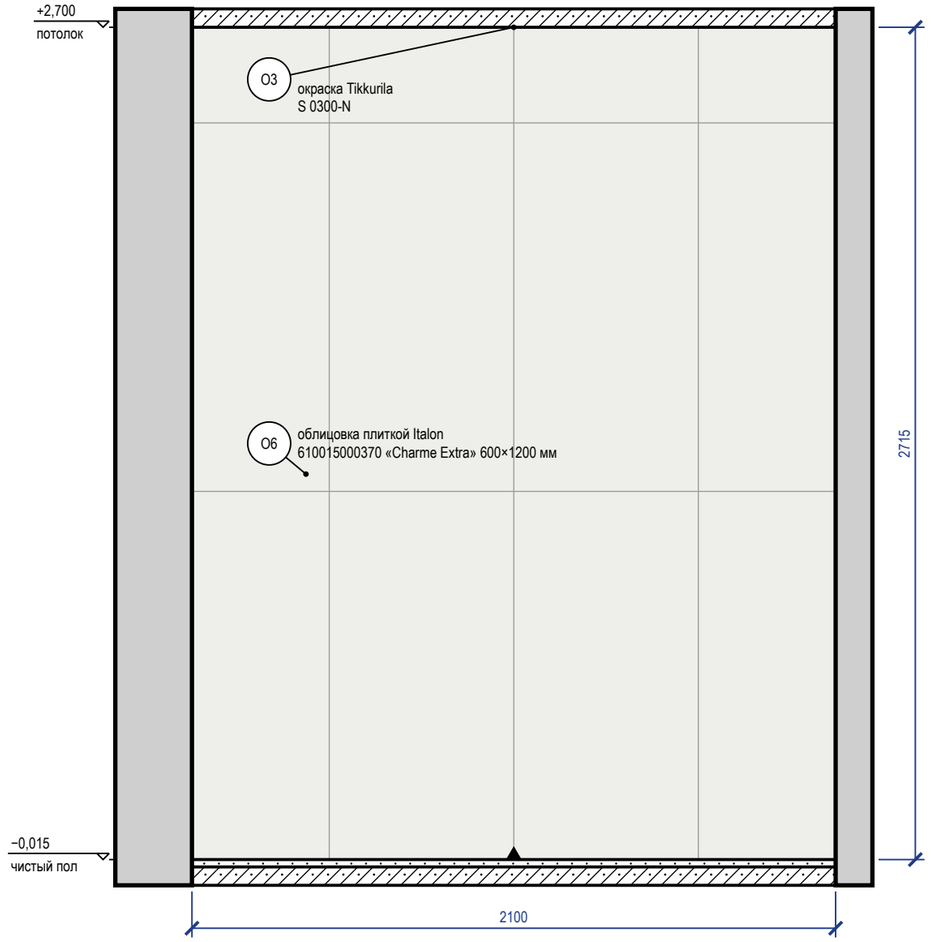

Развёртка стены Б


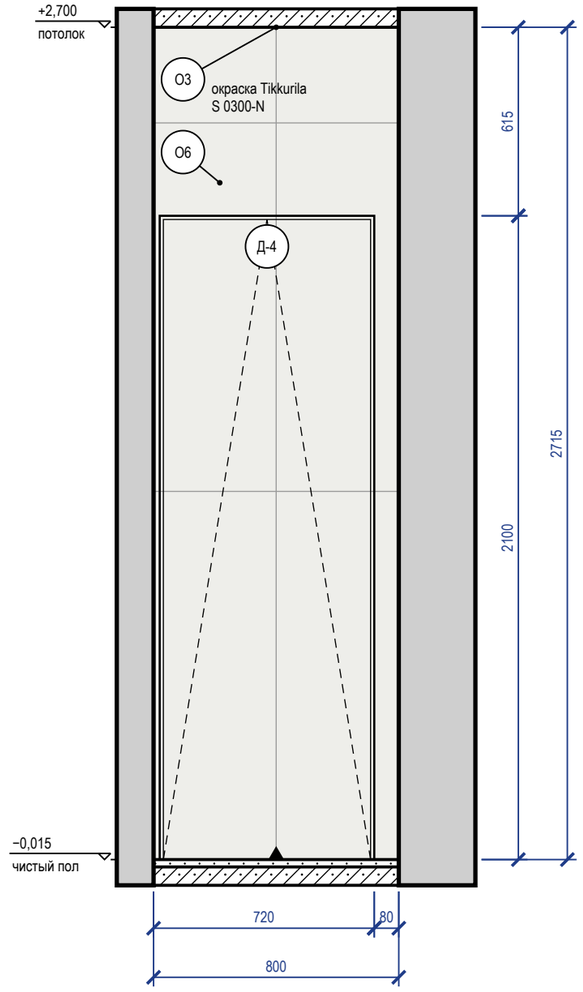


Схема развёрток (М 1:100)

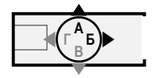

Ведомость отделки (на листе)

Марка	Поверхность	Материал, изделие	Цвет, код	Кол.
О3	потолок	окраска, Tikkurila, глубокоматовая	NCS S 0300-N	1,8 м²
О6	стены	облицовка плиткой, Italon Charme Extra, 600×1200 мм, 610015000370	Italon 610015000370 «Charme Extra»	6,4 м²

Примечания

1. Размеры — в мм от чистовых поверхностей стен; условные обозначения и общие указания — лист 2.
2. Облицовка — по сетке швов, раскладка от оси стены (треугольник у пола); подрезки — по листу раскладки плитки.
3. Гидроизоляция в 2 слоя, заход на стены 200 мм — до облицовки, с актом скрытых работ и тестом проливом (узел — на листе узлов).
4. Двери скрытого монтажа — полотно в плоскости стены, отделка стены по полотну, плинтус прерывается у короба (узел — на листе узлов).


					Проект: Квартира 58 м²
	Лист	№ док.	Подпись	Дата	Развёртки стен А, Б. Санузел (пом. 4)
Дизайнер	Кырлан А.С.			09.10.26	

Стадия	Лист	Листов
П	44	60

выпуск 09.10.2026 № 7efd137e8f · стр. 44 из 60

Правка к этому листу

Развёртка стены В

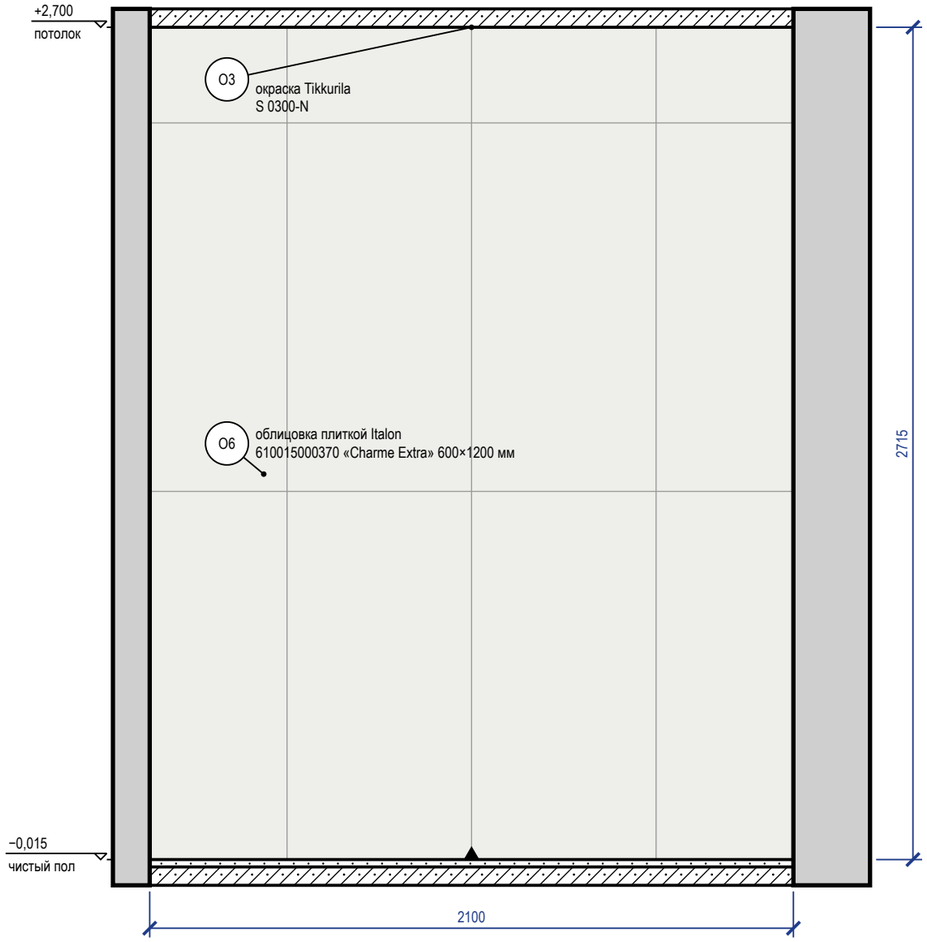

Развёртка стены Г


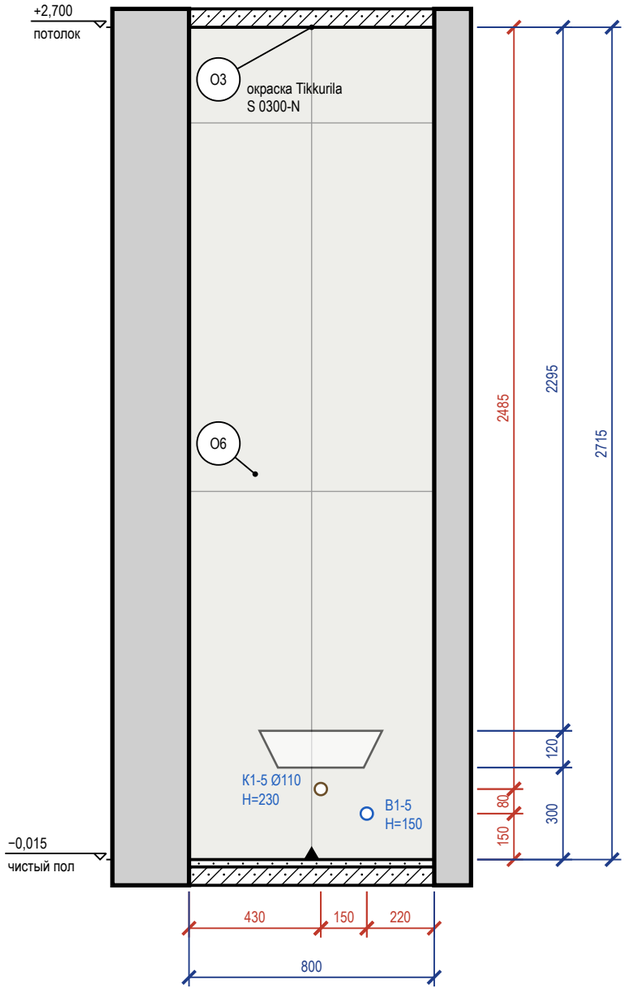


Схема развёрток (М 1:100)

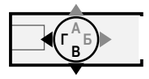

Ведомость отделки (на листе)

Марка	Поверхность	Материал, изделие	Цвет, код	Кол.
О3	потолок	окраска, Tikkurila, глубокоматовая	NCS S 0300-N	1,8 м²
О6	стены	облицовка плиткой, Italon Charme Extra, 600×1200 мм, 610015000370	Italon 610015000370 «Charme Extra»	7,9 м²

Визуализация этой стены — лист 43



Примечания

1. Размеры — в мм от чистовых поверхностей стен; условные обозначения и общие указания — лист 2.
2. Схема мебели, приборов и декора не является технической документацией для производства мебели; габариты — по паспортам изделий.
3. Облицовка — по сетке швов, раскладка от оси стены (треугольник у пола); подрезки — по листу раскладки плитки.
4. Гидроизоляция в 2 слоя, заход на стены 200 мм — до облицовки, с актом скрытых работ и тестом проливом (узел — на листе узлов).

					Проект: Квартира 58 м²
	Лист	№ док.	Подпись	Дата	Развёртки стен В, Г. Санузел (пом. 4)
Дизайнер	Кырлан А.С.			09.10.26	

Стадия	Лист	Листов
П	45	60

выпуск 09.10.2026 № 7efd137e8f · стр. 45 из 60

Правка к этому листу



					Проект: Квартира 58 м²
	Лист	№ док.	Подпись	Дата	
Дизайнер	Кырлан А.С.			09.10.26	Визуализация прихожей

Стадия	Лист	Листов
П	46	60

выпуск 09.10.2026 № 7efd137e8f · стр. 46 из 60

Правка к этому листу



					Проект: Квартира 58 м²
	Лист	№ док.	Подпись	Дата	
Дизайнер	Кырлан А.С.			09.10.26	Визуализация прихожей

Стадия	Лист	Листов
П	47	60

выпуск 09.10.2026 № 7efd137e8f · стр. 47 из 60

Развёртка стены А


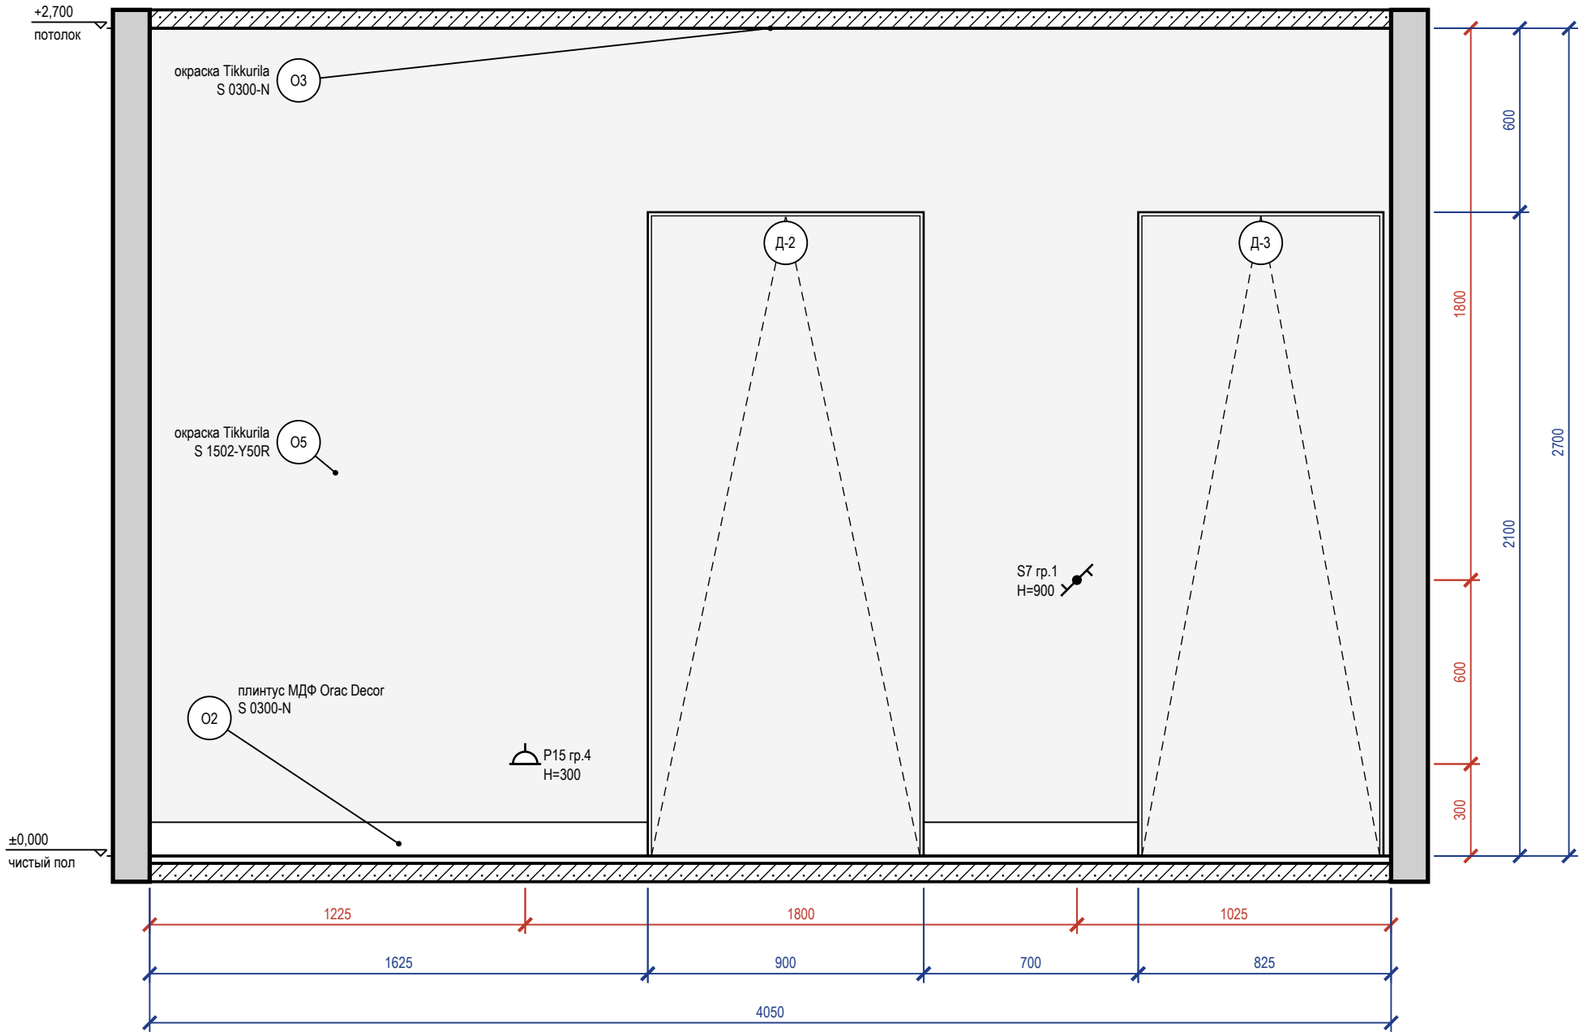


Схема развёрток (М 1:100)

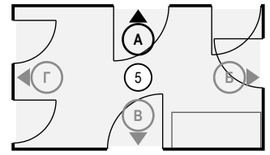

Ведомость отделки (на листе)

Марка	Поверхность	Материал, изделие	Цвет, код	Кол.
О2	плинтус	плинтус МДФ, Orac Decor Luxxus, h 110 мм, SX184, шелковисто-матовая	NCS S 0300-N	2,3 м
О3	потолок	окраска, Tikkurila, глубокоматовая	NCS S 0300-N	9,6 м²
О5	стены	окраска, Tikkurila, шелковисто-матовая, подготовка Q3	NCS S 1502-Y50R	7,4 м²

Визуализация этой стены — лист 46



Примечания

1. Размеры — в мм от чистовых поверхностей стен; условные обозначения и общие указания — лист 2.
2. Двери скрытого монтажа — полотно в плоскости стены, отделка стены по полотну, плинтус прерывается у короба (узел — на листе узлов).

					Проект: Квартира 58 м²
	Лист	№ док.	Подпись	Дата	Развёртка стены А. Прихожая (пом. 5)
Дизайнер	Кырлан А.С.			09.10.26	

Стадия	Лист	Листов
П	48	60

выпуск 09.10.2026 № 7efd137e8f · стр. 48 из 60

Правка к этому листу

Развёртка стены Б


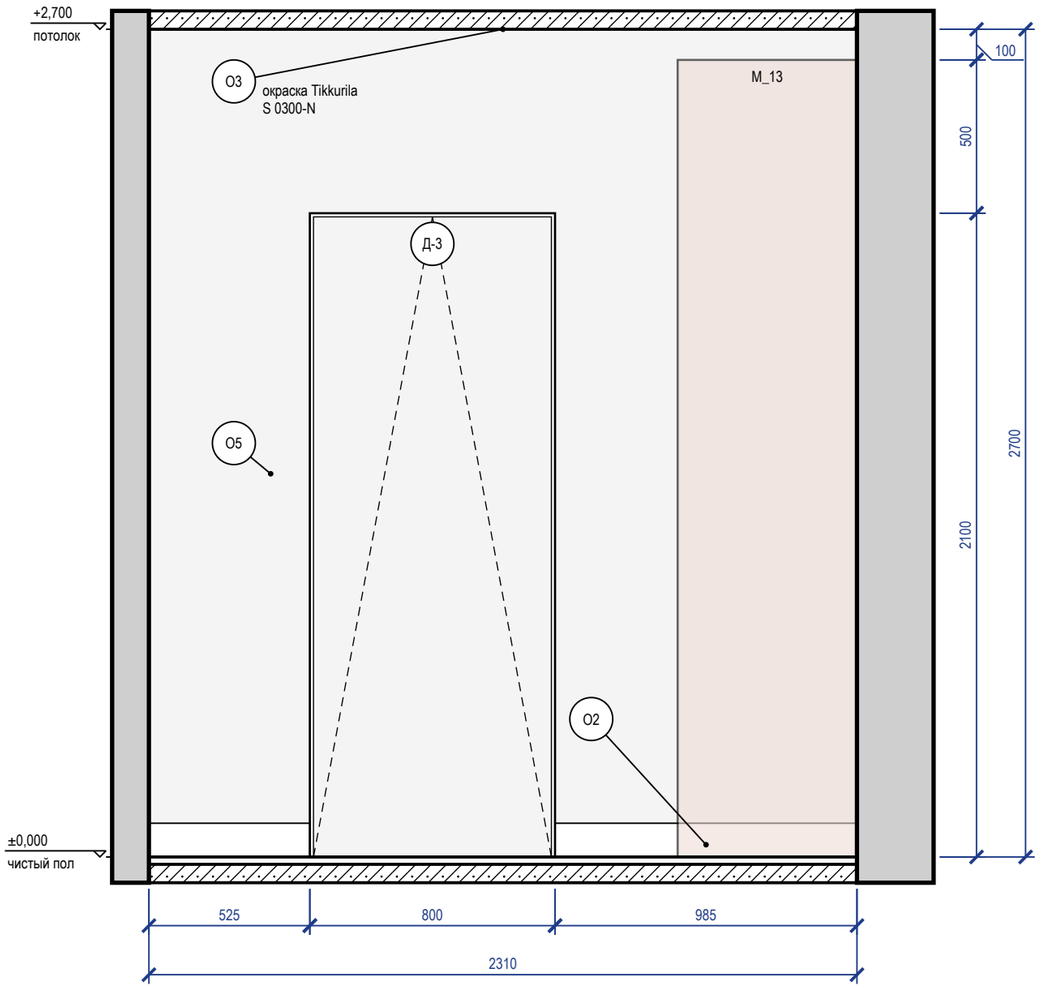


Схема развёрток (М 1:100)

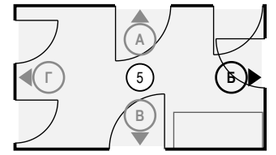

Ведомость отделки (на листе)

Марка	Поверхность	Материал, изделие	Цвет, код	Кол.
О2	плинтус	плинтус МДФ, Orac Decor Luxxus, h 110 мм, SX184, шелковисто-матовая	NCS S 0300-N	1,5 м
О3	потолок	окраска, Tikkurila, глубокоматовая	NCS S 0300-N	9,6 м²
О5	стены	окраска, Tikkurila, шелковисто-матовая, подготовка Q3	NCS S 1502-Y50R	4,6 м²

Примечания

1. Размеры — в мм от чистовых поверхностей стен; условные обозначения и общие указания — лист 2.
2. Двери скрытого монтажа — полотно в плоскости стены, отделка стены по полотну, плинтус прерывается у короба (узел — на листе узлов).

	Лист	№ док.	Подпись	Дата	Проект: Квартира 58 м²			
Дизайнер	Кырлан А.С.			09.10.26	Развёртка стены Б. Прихожая (пом. 5)	Стадия	Лист	Листов
						П	49	60

выпуск 09.10.2026 № 7efd137e8f · стр. 49 из 60

Правка к этому листу

Развёртка стены В


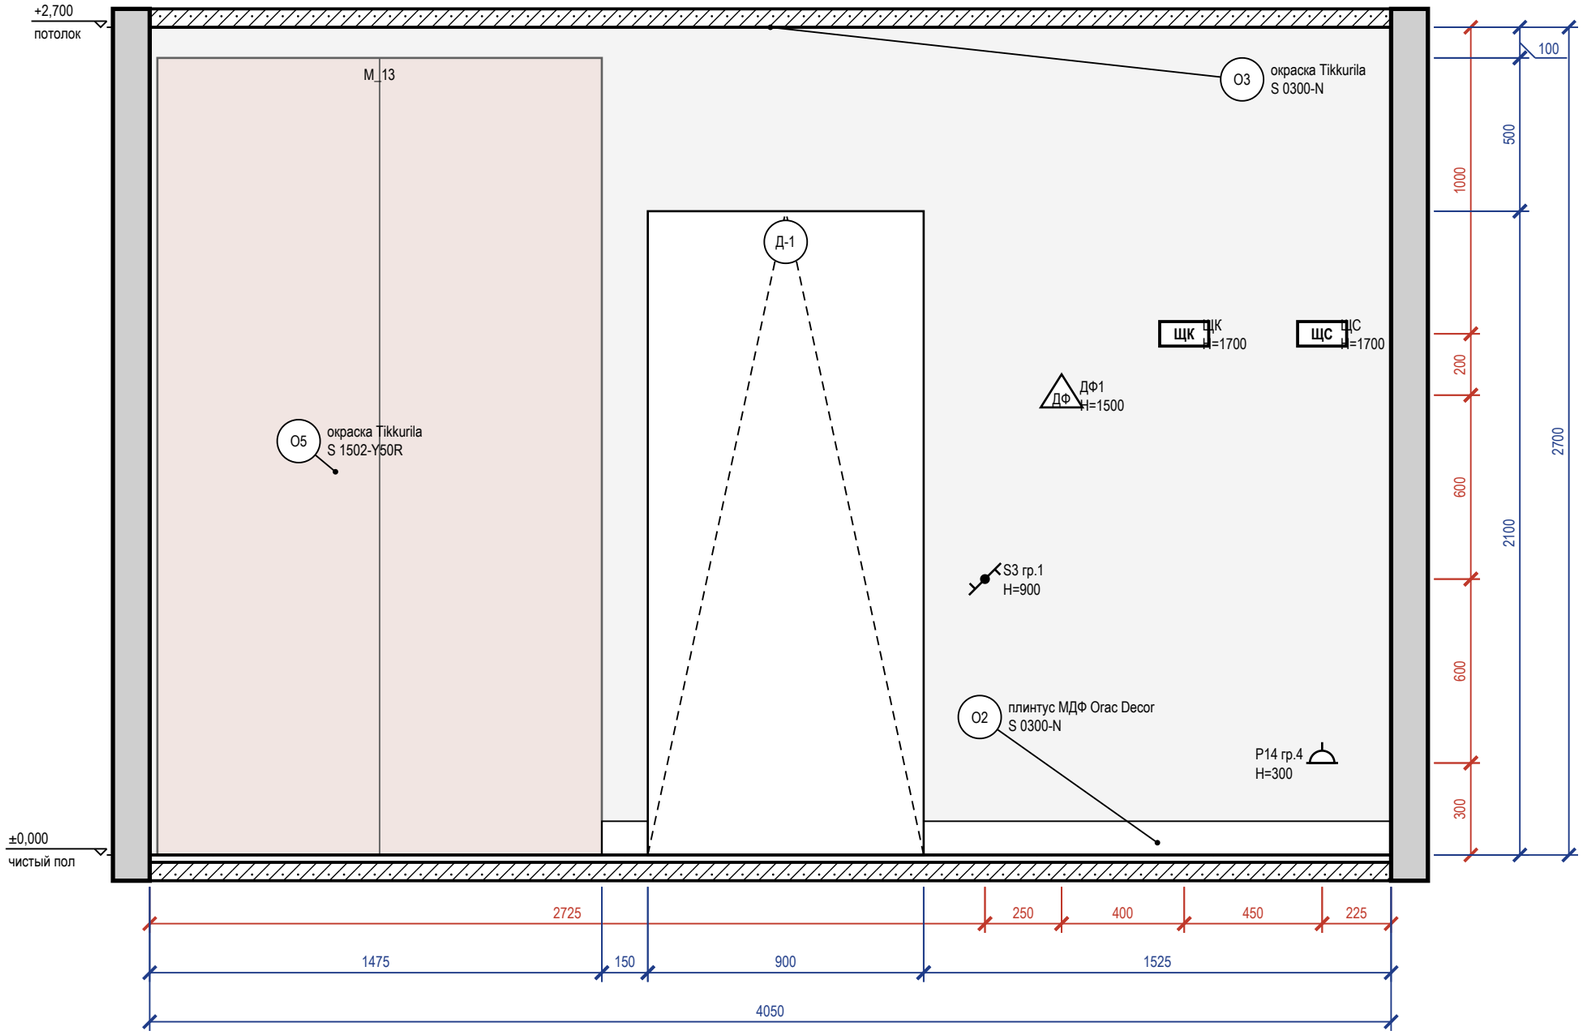


Схема развёрток (М 1:100)

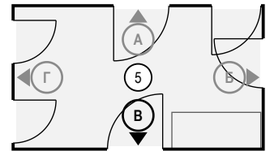

Ведомость отделки (на листе)

Марка	Поверхность	Материал, изделие	Цвет, код	Кол.
О2	плинтус	плинтус МДФ, Orac Decor Luxxus, h 110 мм, SX184, шелковисто-матовая	NCS S 0300-N	1,7 м
О3	потолок	окраска, Tikkurila, глубокоматовая	NCS S 0300-N	9,6 м²
О5	стены	окраска, Tikkurila, шелковисто-матовая, подготовка Q3	NCS S 1502-Y50R	9 м²

Визуализация этой стены — лист 47



Примечания

1. Размеры — в мм от чистовых поверхностей стен; условные обозначения и общие указания — лист 2.

					Проект: Квартира 58 м²
	Лист	№ док.	Подпись	Дата	Развёртка стены В. Прихожая (пом. 5)
Дизайнер	Кырлан А.С.			09.10.26	

Стадия	Лист	Листов
П	50	60

Правка к этому листу

Развёртка стены Г


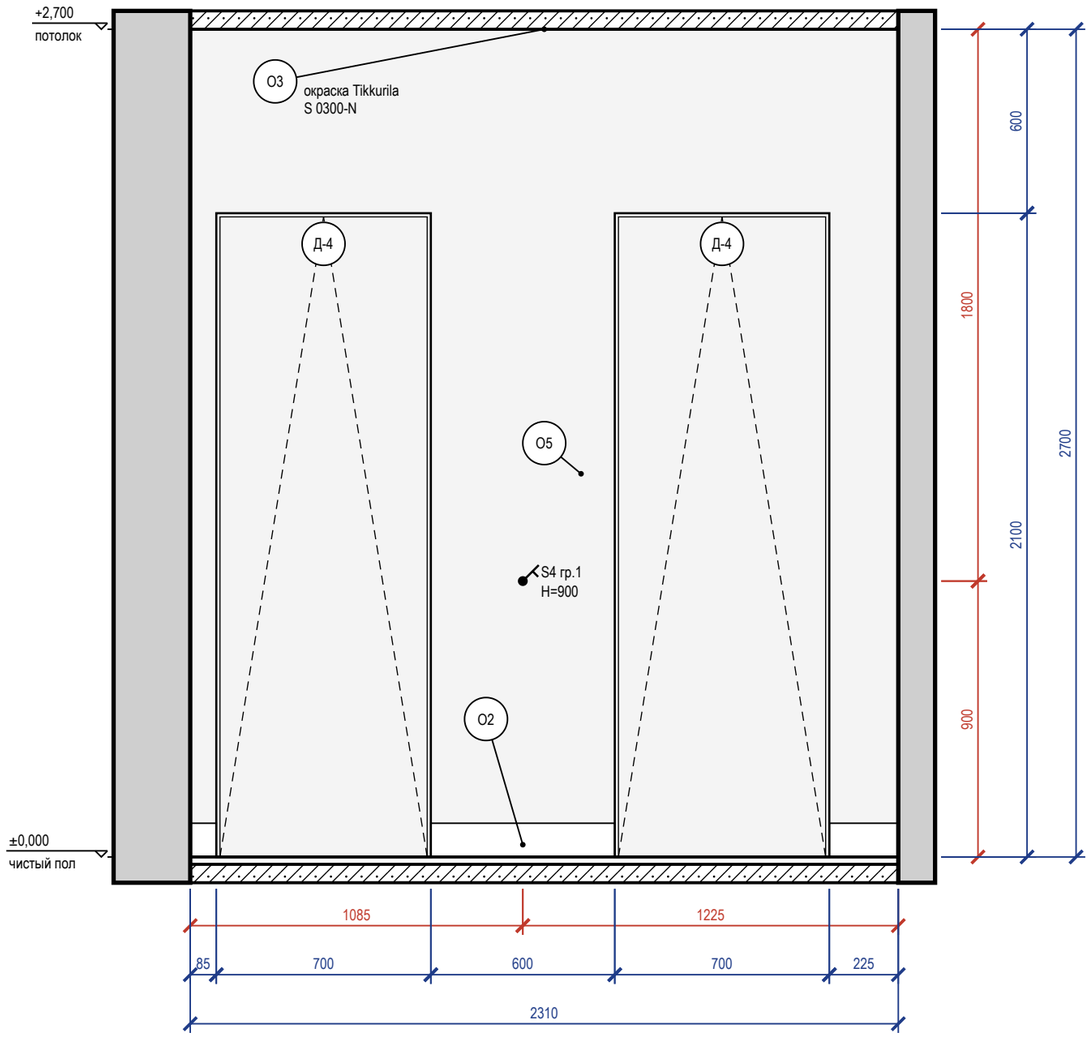


Схема развёрток (М 1:100)

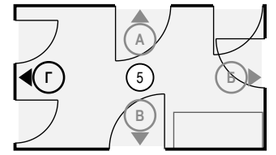

Ведомость отделки (на листе)

Марка	Поверхность	Материал, изделие	Цвет, код	Кол.
О2	плинтус	плинтус МДФ, Orac Decor Luxxus, h 110 мм, SX184, шелковисто-матовая	NCS S 0300-N	0,9 м
О3	потолок	окраска, Tikkurila, глубокоматовая	NCS S 0300-N	9,6 м²
О5	стены	окраска, Tikkurila, шелковисто-матовая, подготовка Q3	NCS S 1502-Y50R	3,3 м²

Примечания

1. Размеры — в мм от чистовых поверхностей стен; условные обозначения и общие указания — лист 2.
2. Двери скрытого монтажа — полотно в плоскости стены, отделка стены по полотну, плинтус прерывается у короба (узел — на листе узлов).

	Лист	№ док.	Подпись	Дата
Дизайнер	Кырлан А.С.			09.10.26

Проект: Квартира 58 м²

Развёртка стены Г. Прихожая (пом. 5)

Стадия	Лист	Листов
П	51	60


Правка к этому листу



					Проект: Квартира 58 м²	
	Лист	№ док.	Подпись	Дата	Визуализация гардеробной	Стадия / Лист / Листов
Дизайнер	Кырлан А.С.			09.10.26		П / 52 / 60

выпуск 09.10.2026 № 7efd137e8f · стр. 52 из 60

Развёртка стены А

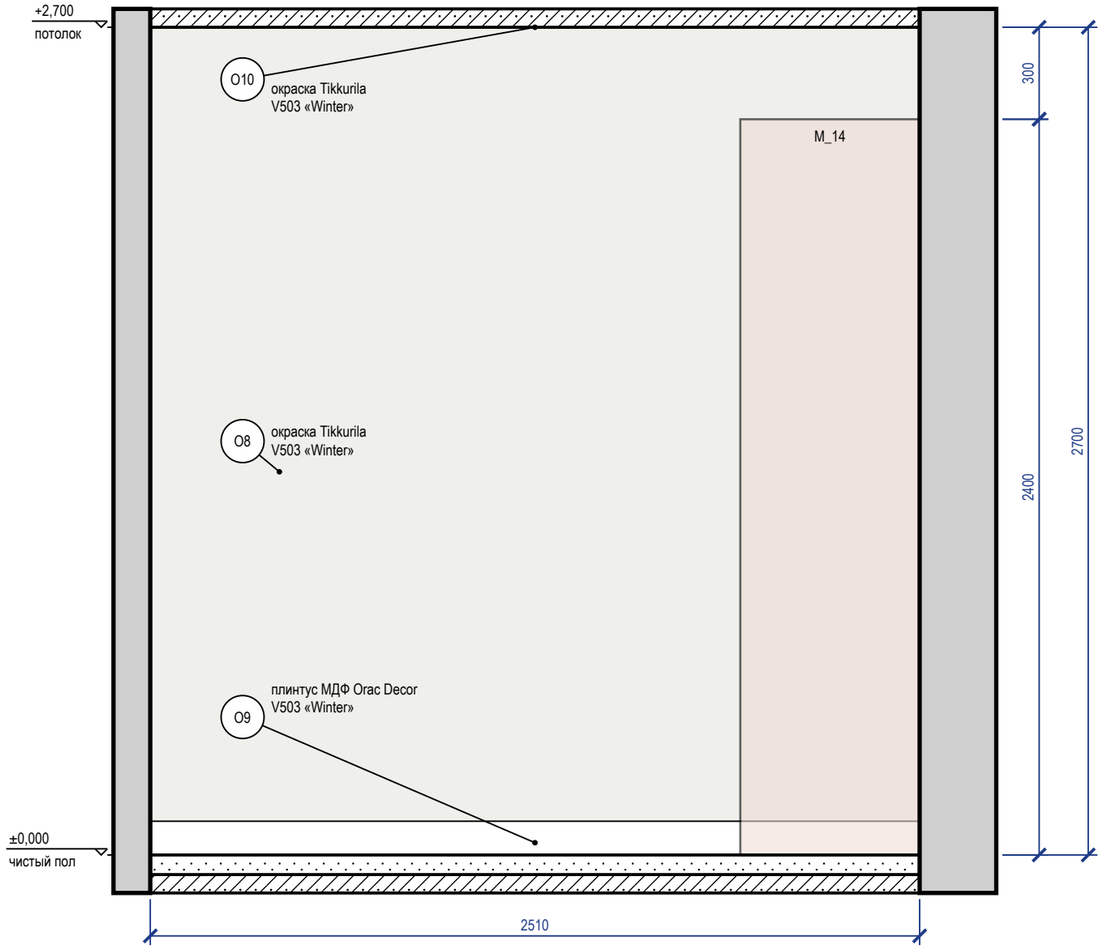

Развёртка стены Б


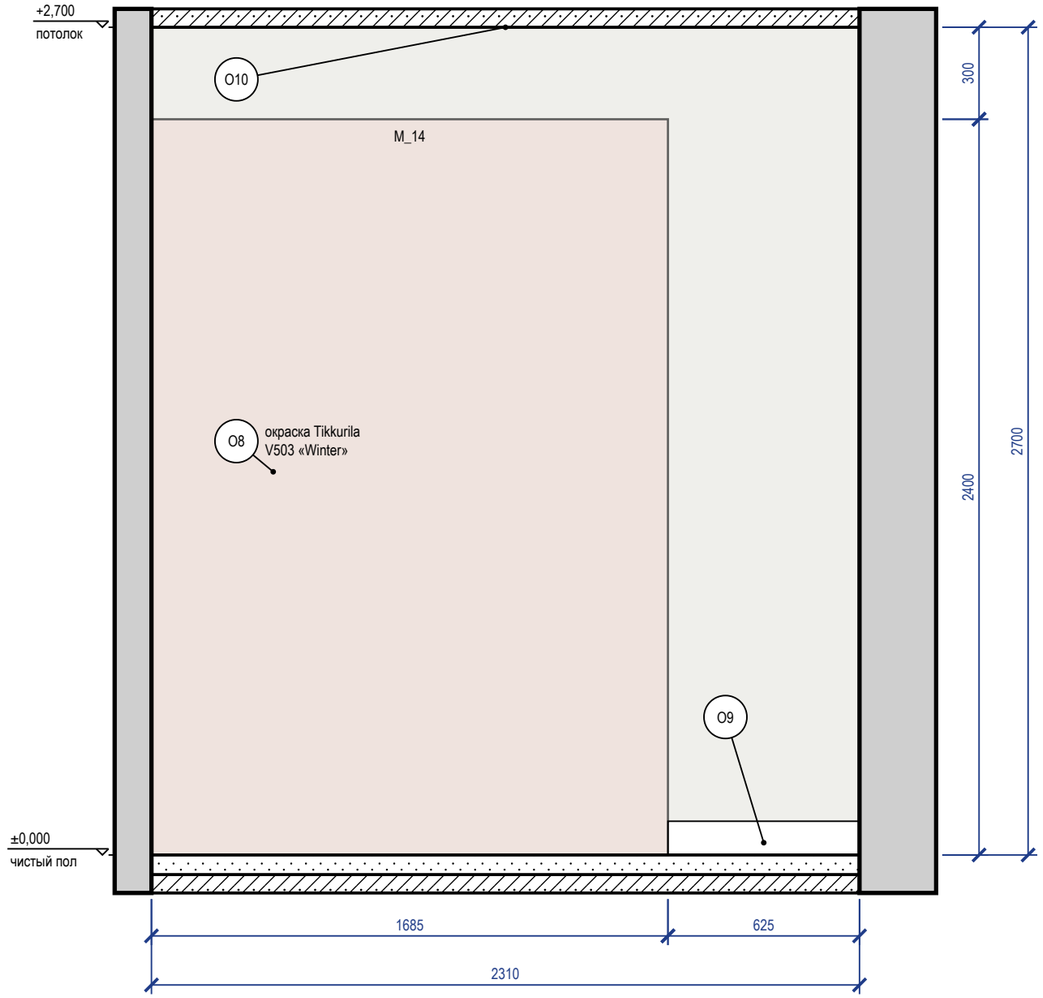



Схема развёрток (М 1:100)

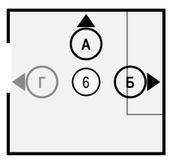

Ведомость отделки (на листе)

Марка	Поверхность	Материал, изделие	Цвет, код	Кол.
О8	стены	окраска, Tikkurila Harmony, матовая, подготовка Q3	Tikkurila V503 «Winter»	13 м²
О9	плинтус	плинтус МДФ, Orac Decor Luxxus, h 110 мм, SX184	Tikkurila V503 «Winter»	3,1 м
О10	потолок	окраска, Tikkurila Anti-Reflex 2, глубокоматовая, подготовка Q3	Tikkurila V503 «Winter»	5,9 м²

Визуализация этой стены — лист 52

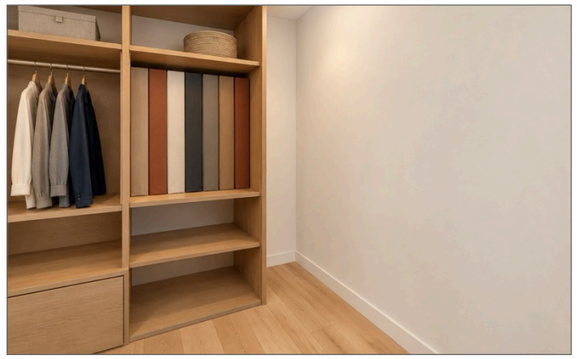

Примечания

1. Размеры — в мм от чистовых поверхностей стен; условные обозначения и общие указания — лист 2.

					Проект: Квартира 58 м²
	Лист	№ док.	Подпись	Дата	Развёртки стен А, Б. Гардеробная (пом. 6)
Дизайнер	Кырлан А.С.			09.10.26	

Стадия	Лист	Листов
П	53	60

выпуск 09.10.2026 № 7efd137e8f · стр. 53 из 60

Правка к этому листу

Развёртка стены Г


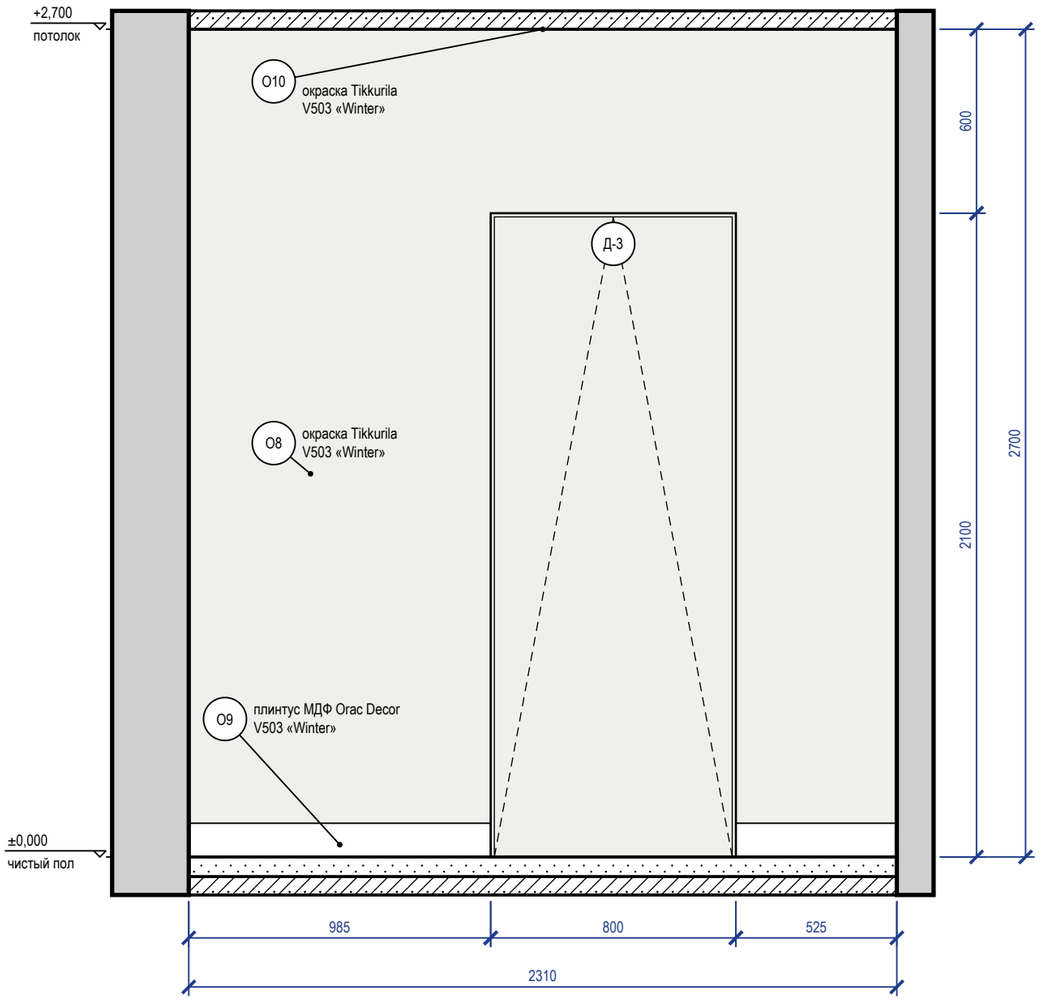


Схема развёрток (М 1:100)

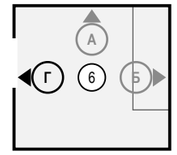

Ведомость отделки (на листе)

Марка	Поверхность	Материал, изделие	Цвет, код	Кол.
О8	стены	окраска, Tikkurila Harmony, матовая, подготовка Q3	Tikkurila V503 «Winter»	4,6 м²
О9	плинтус	плинтус МДФ, Orac Decor Luxxus, h 110 мм, SX184	Tikkurila V503 «Winter»	1,5 м
О10	потолок	окраска, Tikkurila Anti-Reflex 2, глубокоматовая, подготовка Q3	Tikkurila V503 «Winter»	5,9 м²

Примечания

1. Размеры — в мм от чистовых поверхностей стен; условные обозначения и общие указания — лист 2.
2. Двери скрытого монтажа — полотно в плоскости стены, отделка стены по полотну, плинтус прерывается у короба (узел — на листе узлов).


					Проект: Квартира 58 м²
	Лист	№ док.	Подпись	Дата	Развёртка стены Г. Гардеробная (пом. 6)
Дизайнер	Кырлан А.С.			09.10.26	

Стадия	Лист	Листов
П	54	60


выпуск 09.10.2026 № 7efd137e8f · стр. 54 из 60

Правка к этому листу


Вид с фасадами

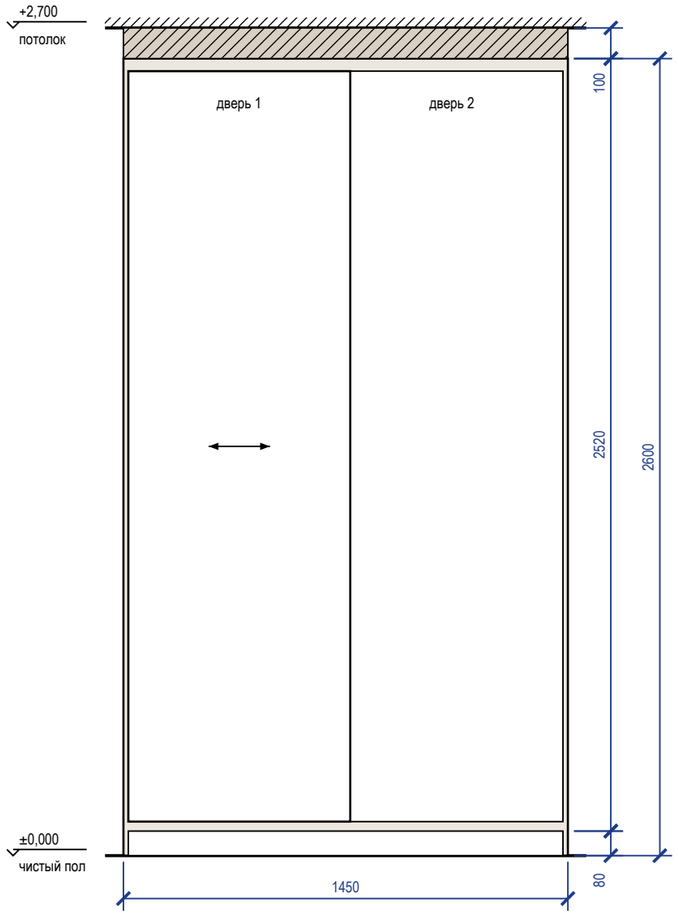


Вид без фасадов

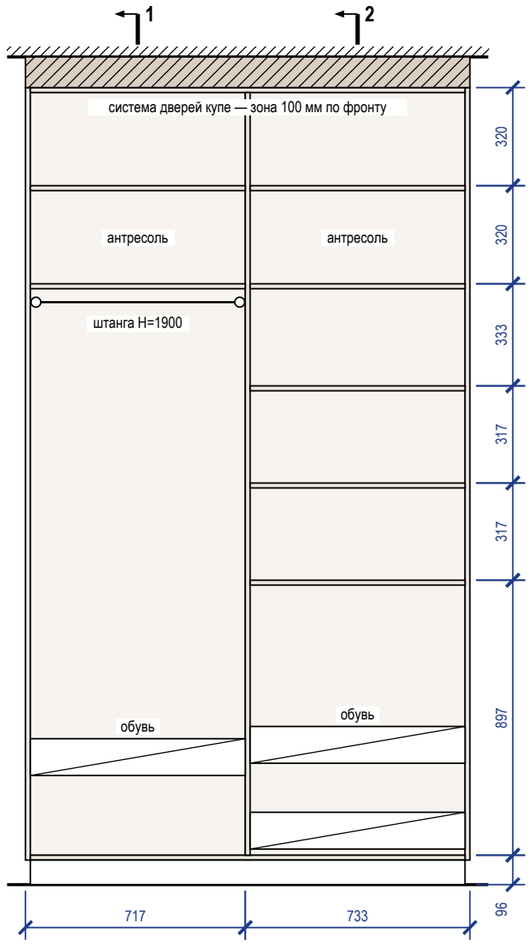

Разрез 1-1

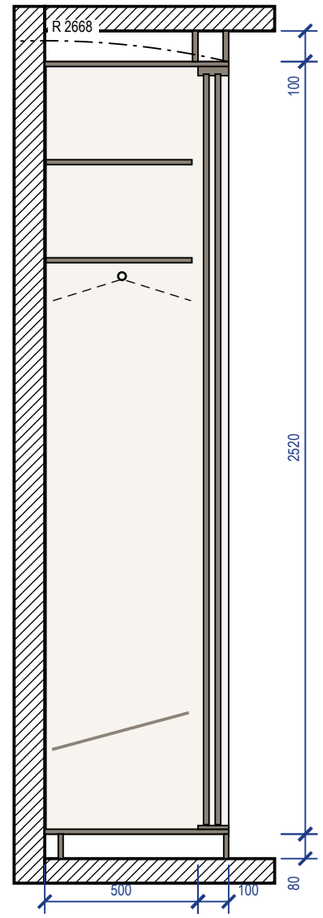


Разрез 2-2

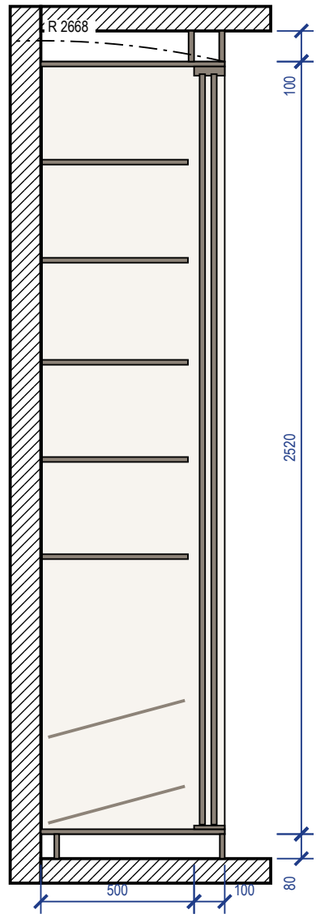

Примечания

1. Размеры — в мм по чистовой отделке; изделие 1450×600×2600 (Ш×Г×В). Перед раскроем — контрольный замер цеха после чистовой отделки стен, пола и потолка.
2. Корпус — ЛДСП 16 мм, задняя стенка ХДФ 4 мм в паз, цоколь 80 мм на регулируемых опорах; двери купе — ЛДСП 10 мм в алюминиевом профиле, нахлёст 30 мм, ширина двери 724 мм, высота — проём минус 40 мм; цвет — по колерной карте.
3. Кромка: скрытые торцы 0,4 мм, видимые 1 мм (ПВХ/АБС).
4. Номинальные зазоры: дверь купе — боковина 3 мм, фасад ящика — стойка 2 мм; ящики внутри купе — с накладкой 30 мм на стойке со стороны нахлёста дверей.
5. Ящики — направляющие полного выдвижения NL 450 (внутренняя глубина 496 мм ≥ NL + 3); присадка по 32-й системе — выполняет цех.
6. Компенсатор 100 мм — короб из ЛДСП по фронту и торцам, подгоняется к потолку при монтаже (припуск 20 мм), крепится к корпусу и к потолку.
7. Подъём корпуса: диагональ боковины $\sqrt{(2600^2 + 600^2)} = 2668$ мм < 2700 мм до потолка — корпус собирается лёжа и поднимается поворотом.
8. Крепление к стене от опрокидывания — уголки 2 шт. к несущему основанию (монтажная схема шкафов).

3D орто

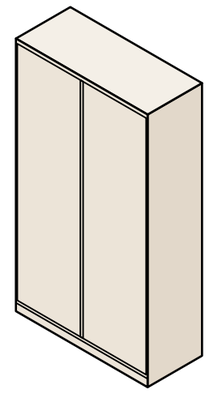


					Проект: Квартира 58 м²		
	Лист	№ док.	Подпись	Дата	Шкаф-купе M_13	Стадия	Лист	Листов
Дизайнер	Кырлан А.С.			09.10.26		П	Д_1	60


выпуск 09.10.2026 № 7efd137e8f · стр. 55 из 60

Правка к этому листу


Общий вид

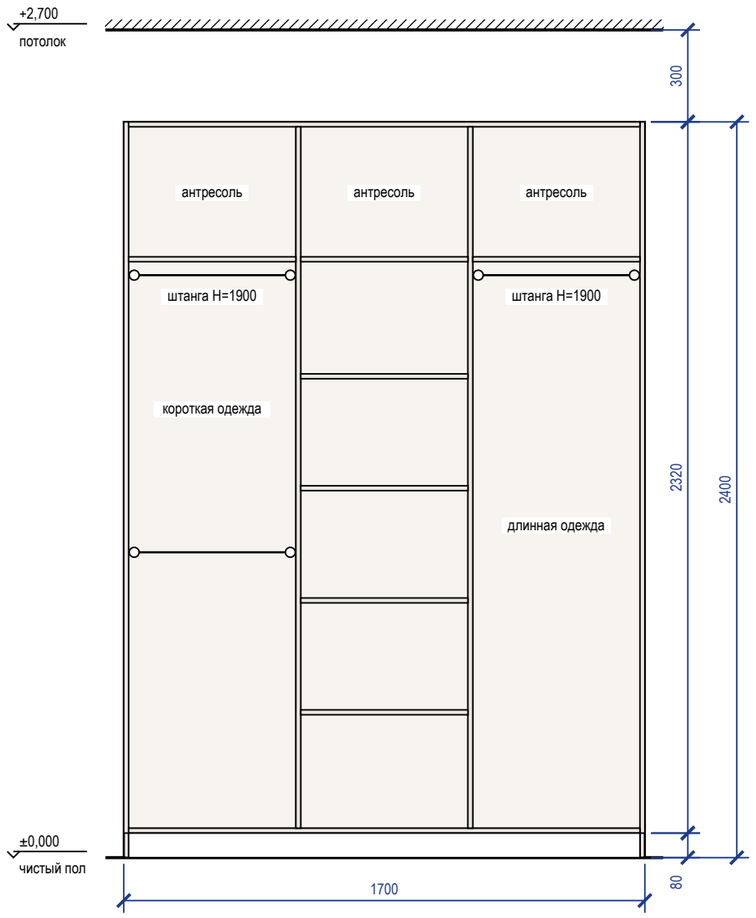


Наполнение, размеры в свету

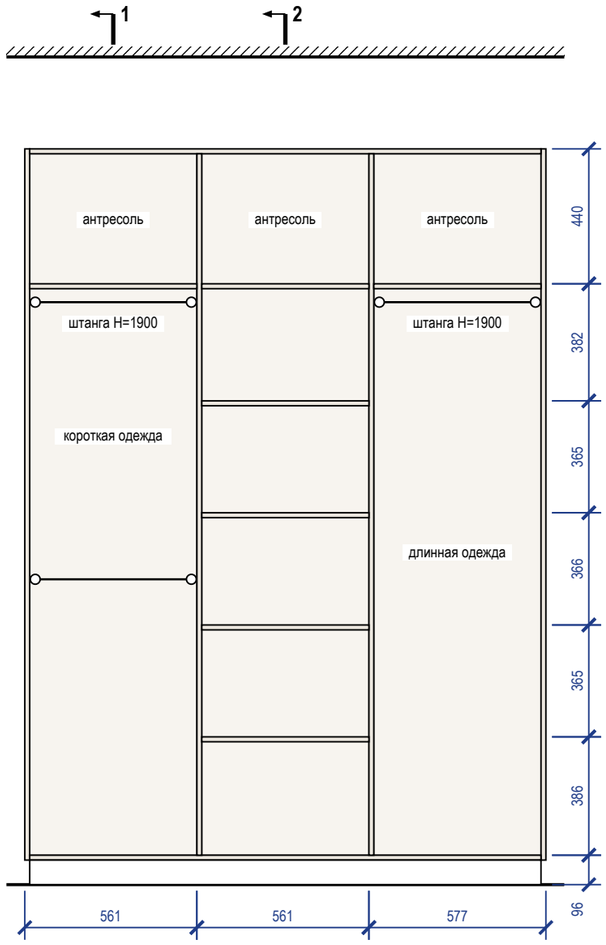

Разрез 1-1

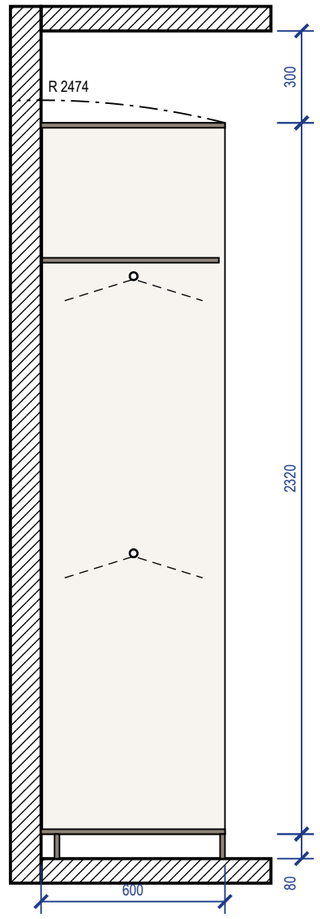


Разрез 2-2

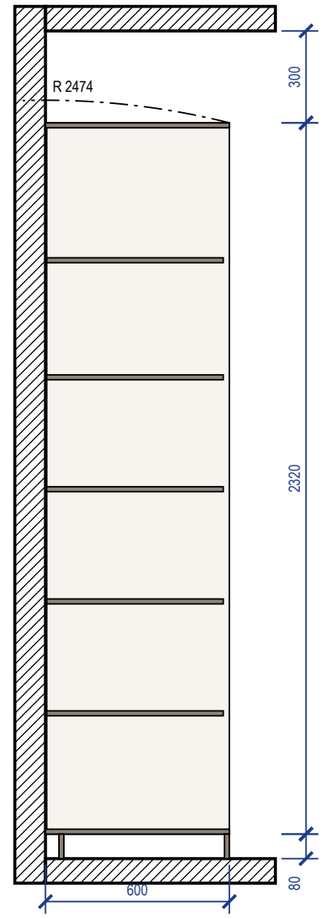

Примечания

1. Размеры — в мм по чистовой отделке; изделие 1700×600×2400 (Ш×Г×В). Перед раскроем — контрольный замер цеха после чистовой отделки стен, пола и потолка.
2. Корпус — ЛДСП 16 мм, задняя стенка ХДФ 4 мм в паз, цоколь 80 мм на регулируемых опорах; открытая система без фасадов, ящики с фасадами.
3. Кромка: скрытые торцы 0,4 мм, видимые 2 мм (ПВХ/АБС).
4. Номинальные зазоры: между фасадами ящиков 3 мм, фасад ящика — стойка 2 мм.
5. Ящики — направляющие полного выдвижения NL 550 (внутренняя глубина 596 мм ≥ NL + 3); присадка по 32-й системе — выполняет цех.
6. Зазор до потолка 300 мм.
7. Подъём корпуса: диагональ боковины $\sqrt{(2400^2 + 600^2)} = 2474$ мм < 2700 мм до потолка — корпус собирается лёжа и поднимается поворотом.
8. Крепление к стене от опрокидывания: крепление к стене, 3 точки; основание стены и шаг анкеров — монтажная схема шкафов.

3D орто

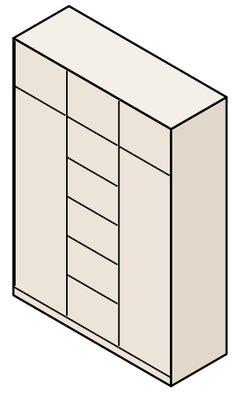


					Проект: Квартира 58 м²	
	Лист	№ док.	Подпись	Дата	Система хранения M_14	Стадия / Лист / Листов
Дизайнер	Кырлан А.С.			09.10.26		П / Д_2 / 60


выпуск 09.10.2026 № 7efd137e8f · стр. 56 из 60

Правка к этому листу


Вид с фасадами

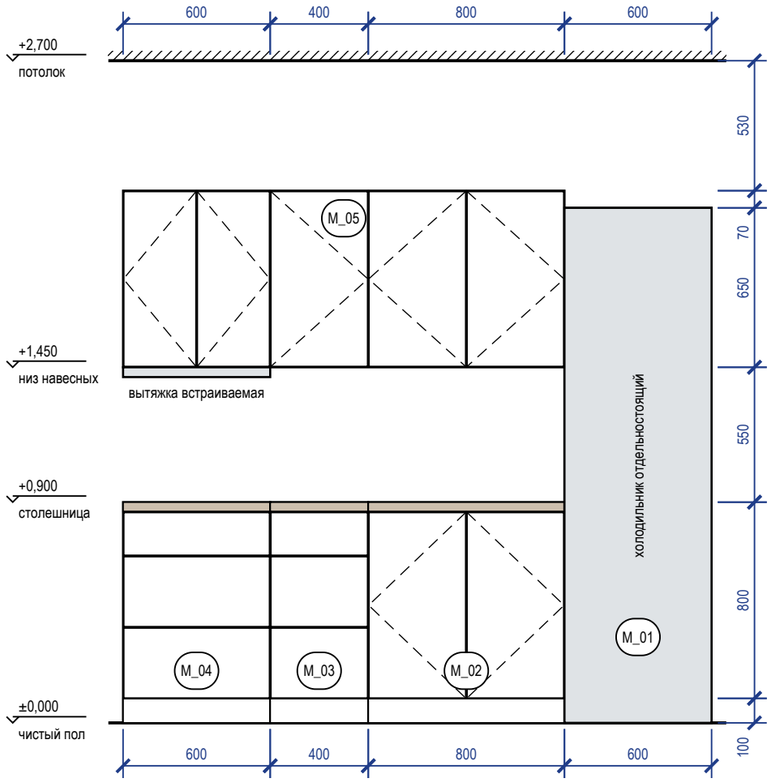


Вид без фасадов (наполнение, выводы)

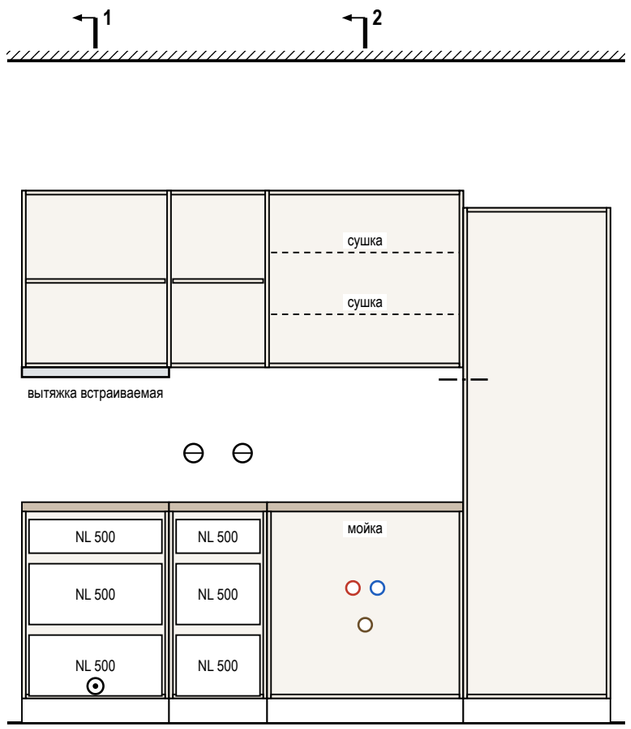


Разрез 1-1

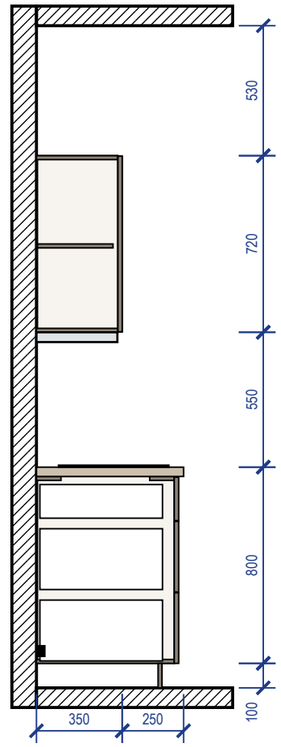

Разрез 2-2

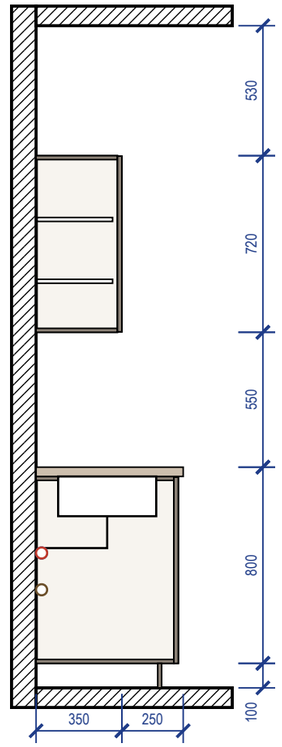

3D орто

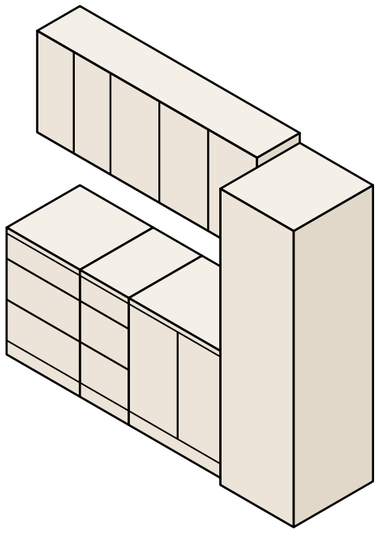

Примечания

1. Размеры — в мм по чистовой отделке, вид из помещения; марки — как на плане расстановки. Перед раскроем — контрольный замер цеха после фартука и пола.
2. Корпуса — ЛДСП 16 мм, задняя стенка ХДФ 4 мм; фасады — МДФ эмаль 18 мм, цвет по колерной карте; столешница 38 мм, свес 20 мм; цоколь 100 мм.
3. Кромка: скрытые торцы 0,4 мм, видимые 1 мм. Номинальные зазоры: между фасадами 3 мм, фасад — столешница 3 мм, фасад — стена не менее 3 мм.
4. Ящики полного выдвижения и петли — с доводчиком; присадка по 32-й системе — выполняет цех.
5. Вытяжка встраивается в навесной модуль над варочной: её низ 510 мм над панелью — меньше 650 мм, модуль поднять или принять вытяжку с допуском по паспорту модели.
6. Ниши техники — по монтажным схемам выбранных моделей: решётка в цоколе и канал за пеналом холодильника, зазор за духовым шкафом, фасад ПММ на двери машины.

					Проект: Квартира 58 м²
	Лист	№ док.	Подпись	Дата	Кухня (пом. 1). Развёртка гарнитура
Дизайнер	Кырлан А.С.			09.10.26	

Стадия	Лист	Листов
П	Д_3	60

выпуск 09.10.2026 № 7efd137e8f · стр. 57 из 60

Правка к этому листу

Ведомость отделки помещений (форма 1 прил. А ГОСТ 21.501-2018)

№	Наименование помещения	Потолок			Стены и перегородки			Низ стен (плинтус)			Пол		Примечание
		Вид отделки	Код цвета	S, м²	Вид отделки	Код цвета	S, м²	Вид отделки	Код цвета	L, м	Вид отделки	S, м²	
1	Кухня-гостиная 21,04 м²	Окраска, Tikkurila, глубокоматовая	NCS S 0300-N	21,04	Окраска, Tikkurila, полуматовая, подготовка Q3	NCS S 1002-Y50R	43,10	Плинтус МДФ h=110 мм, SX184	NCS S 0300-N	17,7	Инженерная доска, IM1861, 1380×190 мм, на клею; тип 1, отм. ЧП ±0,000	21,04	Н стен 2700 (до потолка)
2	Спальня 13,95 м²	Окраска, Tikkurila, глубокоматовая	NCS S 0300-N	13,95	Окраска, Tikkurila, глубокоматовая, подготовка Q3	NCS S 1502-Y50R	36,15	Плинтус МДФ h=110 мм, SX184	NCS S 0300-N	14,2	Инженерная доска, IM1861, 1380×190 мм, на клею; тип 1, отм. ЧП ±0,000	13,95	Н стен 2700 (до потолка)
3	Ванная 2,95 м²	Окраска, Tikkurila, глубокоматовая	NCS S 0300-N	2,95	Облицовка плиткой, 610015000370, 600×1200 мм, клей С2	Italon 610015000370	17,64	нет (облицовка от пола)			Керамогранит, SG651622R, 600×600 мм; тип 2, отм. ЧП −0,015	2,95	Н стен 2715 (до потолка); тёплый пол; гидроизоляция обмазочная, 2 слоя, с заведением на стены 200 мм (по пирогу пола); тест проливом и акт скрытых работ
4	Санузел 1,80 м²	Окраска, Tikkurila, глубокоматовая	NCS S 0300-N	1,80	Облицовка плиткой, 610015000370, 600×1200 мм, клей С2	Italon 610015000370	14,71	нет (облицовка от пола)			Керамогранит, SG651622R, 600×600 мм; тип 2, отм. ЧП −0,015	1,80	Н стен 2715 (до потолка); гидроизоляция обмазочная, 2 слоя, с заведением на стены 200 мм (по пирогу пола); тест проливом и акт скрытых работ
5	Прихожая 9,55 м²	Окраска, Tikkurila, глубокоматовая	NCS S 0300-N	9,55	Окраска, Tikkurila, полуматовая, подготовка Q3	NCS S 1502-Y50R	24,59	Плинтус МДФ h=110 мм, SX184	NCS S 0300-N	8,0	Керамогранит, SG651622R, 600×600 мм; тип 3, отм. ЧП ±0,000	9,55	Н стен 2700 (до потолка)
6	Гардеробная 5,94 м²	Окраска, Tikkurila Anti-Reflex 2, глубокоматовая, 2 слоя, подготовка Q3	Tikkurila V503	5,94	Окраска, Tikkurila Harmony, матовая, 2 слоя, подготовка Q3	Tikkurila V503	24,67	Плинтус МДФ h=110 мм, SX184	Tikkurila V503	9,0	Инженерная доска, IM1861, 1380×190 мм, на клею; тип 4, отм. ЧП ±0,000	5,94	Н стен 2700 (до потолка); плинтус в цвет: стены
	Итого			**55,23**			**160,87**			**48,8**		**55,23**	

Сводка площадей по материалам отделки

Поверхность	Материал / код цвета	Серия	Площадь, м²
Потолок	NCS S 0300-N		49,29
Потолок	Tikkurila V503	Anti-Reflex 2	5,94
Стены	NCS S 1002-Y50R		43,10
Стены	NCS S 1502-Y50R		60,74
Стены	облицовка плиткой 600×1200 мм, Italon 610015000370	610015000370	32,36
Стены	Tikkurila V503	Harmony	24,67

Примечания

1. Площади поверхностей — по чистым граням стен до отделки: стены = периметр × высоту от чистого пола помещения до низа потолка минус проёмы (облицовка плиткой — до верха облицовки); плинтус = периметр минус дверные проёмы; пол и потолок — по площади помещения. Количество плиток по раскладке. Площади помещений — с учётом всех частей помещения; откосы в площадь стен не входят.
2. Акцентные стены — отдельными строками, их площадь вычтена из основной отделки стен помещения.
3. Плинтус — длина по периметру за вычетом дверных проёмов; примыкания к наличникам и встроенной мебели — по развёрткам.
4. Формат плитки — Ш×В×Т (ширина × высота в положении укладки × толщина), мм; на полу — вдоль стен А/В × вдоль стен Б/Г.
5. Коды цвета — по веерам производителей; колеровка каждой краски одной партией, проверка выкраса при свете D65 и при лампах проекта.
6. Уровни подготовки Q1–Q4 — система Knauf, не норма ГОСТ/СП; допуски поверхностей — по СП 71.13330.2017 (действующая редакция).
7. «аналог:» — изделие задано характеристиками, марку и артикул согласовать с заказчиком до закупки.

					Проект: Квартира 58 м²			
	Лист	№ док.	Подпись	Дата	Ведомость отделки помещений	Стадия	Лист	Листов
Дизайнер	Кырлан А.С.			09.10.26		П	С1	60

Правка к этому листу

Поз.	Наименование и техническая характеристика	Тип, марка, обозначение документа	Код продукции	Поставщик	Ед. изм.	Кол.	Образец	Примечание
	Лакокрасочные материалы							
1	Краска интерьерная водно-дисперсионная акриловая для стен, полуматовая, класс мокрого истирания 1 по EN 13300, база A; цвет NCS S 1002-Y50R, колеровка машинная	Tikkurila		Tikkurila	л	12,6		поз. К1 колерной карты; пом. 1; S = 43,1 м² × 2 сл. × 0,12 л/м² = 10,3 л, +10 % и 0,5 л на подкраску → ≥ 11,9 л; тара 1 × 9 л + 1 × 2,7 л + 1 × 0,9 л
2	Краска интерьерная водно-дисперсионная для потолков, глубокоматовая, класс мокрого истирания 1 по EN 13300, база A; цвет NCS S 0300-N, колеровка машинная	Tikkurila		Tikkurila	л	9,9		поз. К2 колерной карты; пом. 1, 3, 4, 5; S = 35,3 м² × 2 сл. × 0,12 л/м² = 8,5 л, +10 % и 0,5 л на подкраску → ≥ 9,8 л; тара 1 × 9 л + 1 × 0,9 л
3	Краска интерьерная водно-дисперсионная акриловая для стен, глубокоматовая, класс мокрого истирания 2 по EN 13300, база A; цвет NCS S 1502-Y50R, колеровка машинная	Tikkurila		Tikkurila	л	10,8		поз. К4 колерной карты; пом. 2; S = 36,2 м² × 2 сл. × 0,12 л/м² = 8,7 л, +10 % и 0,5 л на подкраску → ≥ 10,0 л; тара 1 × 9 л + 2 × 0,9 л
4	Краска интерьерная водно-дисперсионная для потолков, глубокоматовая, класс мокрого истирания 2 по EN 13300, база A; цвет NCS S 0300-N, колеровка машинная	Tikkurila		Tikkurila	л	4,5		поз. К5 колерной карты; пом. 2; S = 13,9 м² × 2 сл. × 0,12 л/м² = 3,3 л, +10 % и 0,5 л на подкраску → ≥ 4,2 л; тара 1 × 2,7 л + 2 × 0,9 л
5	Краска интерьерная водно-дисперсионная акриловая для стен, полуматовая, класс мокрого истирания 1 по EN 13300, база A; цвет NCS S 1502-Y50R, колеровка машинная	Tikkurila		Tikkurila	л	7,2		поз. К8 колерной карты; пом. 5; S = 24,6 м² × 2 сл. × 0,12 л/м² = 5,9 л, +10 % и 0,5 л на подкраску → ≥ 7,0 л; тара 2 × 2,7 л + 2 × 0,9 л
6	Краска интерьерная водно-дисперсионная акриловая для стен, матовая, класс мокрого истирания 1 по EN 13300, база A; цвет Tikkurila V503 «Winter», колеровка машинная	Tikkurila Harmony		Tikkurila	л	7,2		поз. К9 колерной карты; пом. 6; S = 24,7 м² × 2 сл. × 0,12 л/м² = 5,9 л, +10 % и 0,5 л на подкраску → ≥ 7,0 л; тара 2 × 2,7 л + 2 × 0,9 л
7	Краска интерьерная водно-дисперсионная акриловая для потолков, глубокоматовая, класс мокрого истирания 2 по EN 13300, база A; цвет Tikkurila V503 «Winter», колеровка машинная	Tikkurila Anti-Reflex 2		Tikkurila	л	2,7		поз. К10 колерной карты; пом. 6; S = 5,9 м² × 2 сл. × 0,12 л/м² = 1,4 л, +10 % и 0,5 л на подкраску → ≥ 2,1 л; тара 1 × 2,7 л
8	Акрил, полуматовая в цвет NCS S 0300-N — окраска плинтуса	аналог по характеристикам			л	1,4		поз. К3; пом. 1, 2, 5; L = 39,9 м, S = 5,0 м² × 2 сл. × 0,12 л/м² + 10 %; продукт подобрать в веере NCS
9	Краска для МДФ и дерева в цвет Tikkurila V503 «Winter» — окраска плинтуса; блеск не ниже блеска стен	марка не задана			л	0,5		поз. К11; пом. 6; L = 9,0 м, S = 1,1 м² × 2 сл. × 0,12 л/м² + 10 %; продукт подобрать в веере Tikkurila
10	Грунтовка акриловая под окраску стен и потолков — из системы производителя краски	по системе краски			м²	184		площадь окраски стен, акцентов и потолков; 1 слой перед окраской; расход — по ТУ грунтовки
	Плитка и керамогранит							
11	SG651622R, 600×600 мм, противоскольжение R10	SG651622R		Kerama Marazzi	м²	19,44		шов 2 мм; Ванная, пол; Санузел, пол; Прихожая, пол; по раскладке 48 шт (S = 14,30 м²), с запасом 54 шт
12	610015000370, 600×1200 мм	610015000370		Italon	м²	19,41		3. Ванная, стены; раскладка не выполнена — S = 17,64 м² + 10 %; клей и затирка — по раскладке
13	610015000370, 600×1200 мм	610015000370		Italon	м²	16,19		4. Санузел, стены; раскладка не выполнена — S = 14,71 м² + 10 %; клей и затирка — по раскладке
	Напольные покрытия							
14	IM1861, класс 33, рабочий слой 4 мм, эмиссия E1, укладка на клей	IM1861		Quick-Step	м²	37,5		пом. 1, 2; S = 34,99 м² + 7 % (прямая укладка); к заказу — кратно упаковке
15	IM1861, рабочий слой 4 мм, эмиссия E1, укладка на клей	IM1861		Quick-Step	м²	6,4		пом. 6; S = 5,94 м² + 7 % (прямая укладка); к заказу — кратно упаковке
16	Клей для паркета и инженерной доски, эластичный (СМП / полиуретановый)	по рекомендации производителя доски			м²	41		площадь приклейки; расход и шпатель — по ТУ клея
	Погонажные изделия							
17	SX184, h = 110 мм, крепление к стене, окраска в цвет NCS S 0300-N	SX184		Orac Decor	м	54		пом. 1, 2, 5, 6; L = 48,8 м (периметр без дверных проёмов) + 10 % на подрезку; в штуках — по длине планки
	Смеси и материалы для облицовки							
18	Затирка для швов плитки	аналог по характеристикам			кг	1,5		по раскладке (a+b)/(a·b) × шов × t × 1,6 + 10 %
19	Клей плиточный C2 S1 по EN 12004, слой 5 мм	аналог по характеристикам			кг	37		2 меш. по 25 кг; 1,5 кг/м² на 1 мм слоя + 10 %
20	Клей плиточный C2 по EN 12004, слой 5 мм	аналог по характеристикам			кг	78		4 меш. по 25 кг; 1,5 кг/м² на 1 мм слоя + 10 %
21	Лента демпферная по периметру пола из плитки	аналог по характеристикам			м	21,2		периметр без дверных проёмов + 10 %

Примечания

1. Количества — из геометрии проекта: площади поверхностей по чистым граням стен до отделки (те же, что в ведомости отделки и колерной карте), плитка, клей и затирка — по раскладке плиточника; в графе «Кол.» — к заказу, с запасом.
2. Краска: расход 0,12 л/м² на слой в 2 слоя, если по ТУ не задан иной; запас 10 % и 0,5 л на подкраску каждого кода. Один код — одна партия, колеровка машинная в колеровочном центре бренда; в заказ — только после утверждения выкраса (колерная карта). Фасовка — по каталогу бренда на дату выпуска; к заказу — не меньше расчётного объёма.
3. «Аналог по характеристикам» — допускается изделие другого производителя с характеристиками не ниже указанных, по согласованию с автором проекта.
4. Графы «Код продукции» и «Масса 1 ед.» не заполнены: коды по классификатору продукции не присвоены, масса единицы до 25 кг (ГОСТ 21.110-2013).
5. Грунтовка и клей для доски указаны площадью обработки; объём — по ТУ выбранного продукта.


					Проект: Квартира 58 м²
	Лист	№ док.	Подпись	Дата	
Дизайнер	Кырлан А.С.			09.10.26	Спецификация отделочных материалов

Стадия	Лист	Листов
П	С2	60

Правка к этому листу


1 Порог 15 мм: мокрая зона — жилое помещение (М 1:5)

Применение: двери Д-4

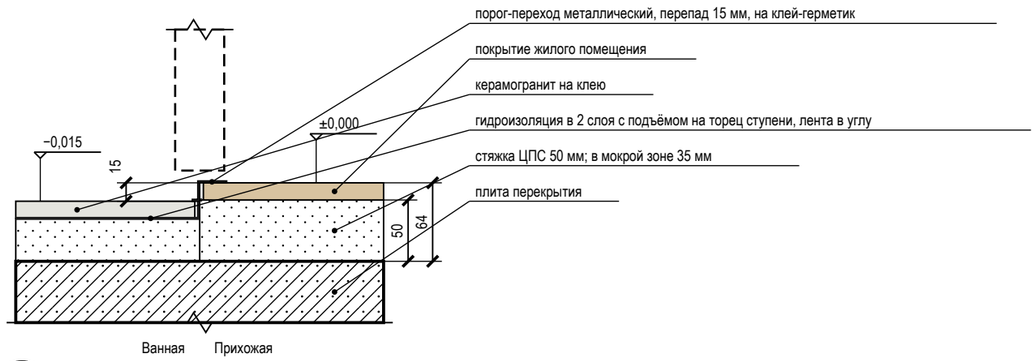


2 Дверь скрытого монтажа в плоскости стены, плинтус (М 1:5)

Применение: двери Д-2, Д-3, Д-4

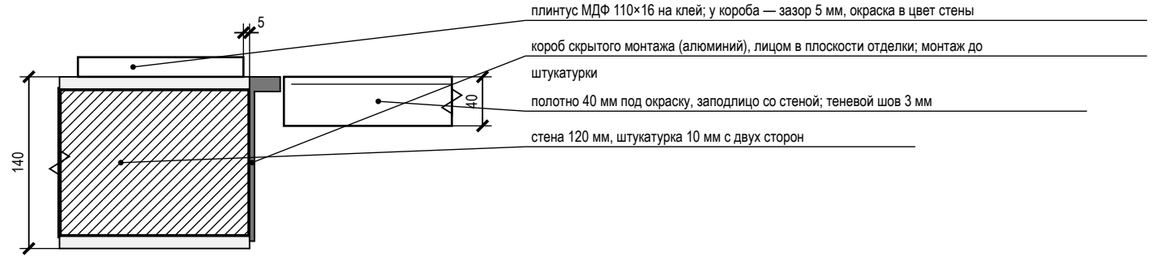


3 Короб стояков К1-1 с люком и звукоизоляцией (М 1:10)

Применение: пом. 3

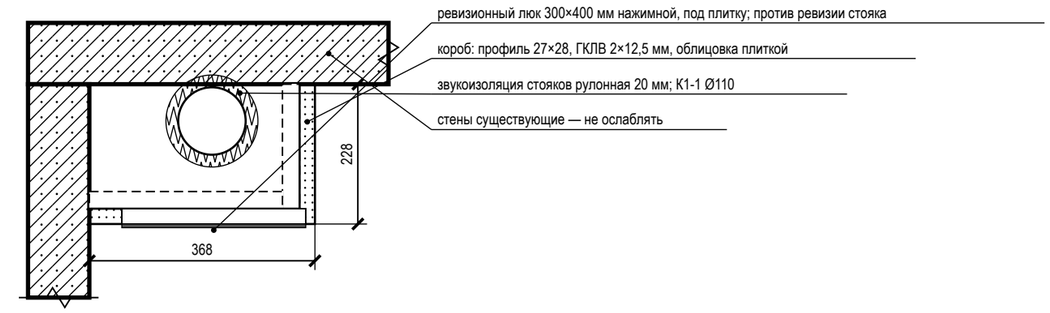


4 Гидроизоляция санузла: заход на стены 200 мм, примыкание ванны (М 1:20)

Применение: пом. 3, 4

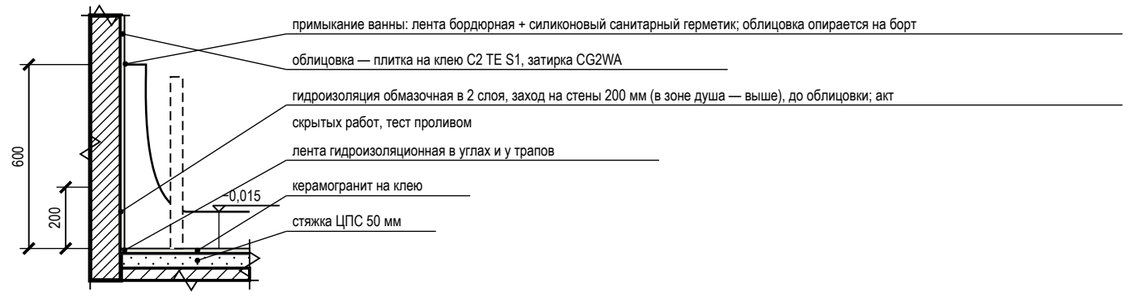

5 Плинтус МДФ 110×16 мм у окрашенной стены (М 1:10)

Применение: пом. 1, 2, 5, 6

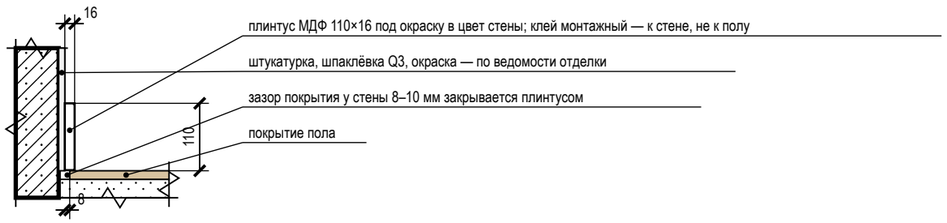

Условные обозначения

- железобетон (плита, стены)
- кладка, перегородка
- стяжка, раствор
- гипсокартон ГКЛВ
- звукоизоляция, эластичный заполнитель
- плитка, керамогранит на клею
- инженерная доска (покрытие пола)
- металлический профиль (порог, Т-профиль, короб двери)
- гидроизоляция (обмазочная, лента)

Примечания

1. Узлы — типовые решения проекта для мест, отмеченных выносками на листе схемы расположения развёрток и узлов; размеры — в мм, отметки — в м от ±0,000.
2. Узлы с гидроизоляцией, закладными и коробами скрытого монтажа принимаются по актам скрытых работ до закрытия отделкой; гидроизоляция — после теста проливом (24 ч).
3. Марки изделий (порог, Т-профиль, короб скрытой двери, люк) — по спецификациям; замена — на аналог с теми же габаритами по согласованию с автором проекта.

					Проект: Квартира 58 м²
	Лист	№ док.	Подпись	Дата	Узлы
Дизайнер	Кырлан А.С.			09.10.26	

Стадия	Лист	Листов
П	С3	60

выпуск 09.10.2026 № 7efd137e8f · стр. 60 из 60