LINEA

РАБОЧАЯ ДОКУМЕНТАЦИЯ

Квартира 65 м²

Шифр комплекта ГД-2026-007-АИ

Стадия РП

Дата выпуска 09.10.2026

ПРЕДВАРИТЕЛЬНО · не для производства работ
открыто пунктов: 4 (реестр — л. 5)



ДИЗАЙНЕР

Кырлан Александр Сергеевич

выпуск 09.10.2026 № 147dabfd23 · стр. 1 из 110

Содержание

ПРЕДВАРИТЕЛЬНО · не для производства работ · открыто пунктов: 4 (реестр — л. 5)

03 Общие данные 10 л.

13 Архитектурные решения 3 л.

17 Планировочное решение 4 л.

22 Электрооборудование 7 л.

30 Отопление и вентиляция 2 л.

33 Водоснабжение и канализация 4 л.

38 Потолки и ГКЛ-конструкции 3 л.

42 Полы и отделка 7 л.

50 Декор и текстиль 12 л.

63 Развёртки и узлы 20 л.

84 Смета 7 л.

92 Визуализации 18 л.

ДИЗАЙН-ПРОЕКТ ИНТЕРЬЕРА

Квартира 65 м²

Скандинавский

65,24 м²

светло · спокойно · уютно (hygge) · естественно · функционально · в меру (lagom)

Палитра из: тёплые нейтрали NCS (стены по ведомости — S 1002-Y50R / S 1502-Y50R близки к ним), акцент — пыльный синий в текстиле.

ПАЛИТРА 60 / 30 / 10

NCS S 0500-N	NCS S 1500-N	NCS S 2002-Y	NCS S 4010-R90B
60 %	30 %	30 %	10 %



B1 · Вид сверху (3D): планировка с мебелью, текстилем и декором

ОБЪЕКТ	ОБЩАЯ ПЛОЩАДЬ	ПОМЕЩЕНИЙ
Квартира 65 м²	65,24 м²	9, из них жилых 3
СТИЛЬ	**СТАДИЯ**	**ШИФР**
Скандинавский	Рабочий проект · предварительно	ГД-2026-007-АИ

АВТОР ПРОЕКТА

Кырлан Александр Сергеевич

Октябрь 2026

Изм.	Кол.уч	Лист	№ док.	Подп.	Дата
Разраб.		Кырлан А.С.			09.10.26
Пров.					
ГИП					
Н. контр.					
Утв.					

ГД-2026-007-АИ

Квартира 65 м²

Общая площадь 65,24* м² · * размеры со скана, не замерены (реестр — п. 5, К-1)

Дизайн-проект интерьера	Стадия	Лист	Листов
	РП	1	79
Титульный лист М 6/м	Кырлан Александр Сергеевич		

выпуск 09.10.2026 № 147dabfd23 · стр. 3 из 110

Общие данные

Комплект ГД-2026-007-АИ · Квартира 65 м² после реконструкции

Ведомость рабочих чертежей основного комплекта ГД-2026-007-АИ

Лист	Наименование	Примечание
1	Титульный лист	
2	Общие данные	
3	Общие данные	
4	Общие данные	
5	Открытые вопросы, принятые допущения и конфликты	
6	Задание на контрольный обмер и обследование. Лист 1 из 2	
7	Задание на контрольный обмер и обследование. Лист 2 из 2	
8	График закупок и работ. Лист 1 из 3	
9	График закупок и работ. Лист 2 из 3	
10	График закупок и работ. Лист 3 из 3	
11	Обмерный план	
12	План демонтажа и монтажа перегородок	
13	План дверей и ведомость заполнения проёмов	
14	Концепция интерьера	
15	План расстановки мебели	
16	Спецификация мебели и оборудования	
17	Спецификация мебели и оборудования (продолжение)	
18	План розеток и электровыводов	
19	План освещения	
20	План выключателей и схема включения	
21	Ведомость электроточек и изделий	
22	Однолинейная схема щита	
23	План принципиальных трасс	
24	План слаботочных сетей	
25	План вентиляции	
26	План отопления	
27	План выводов сантехники	Допущения и предложения на листе. См. лист открытых вопросов (лист 5).
28	Схема разводки водопровода и канализации	
29	Спецификация сантехнического оборудования	
30	Спецификация светильников и сценарии освещения	

Ведомость рабочих чертежей основного комплекта ГД-2026-007-АИ (продолжение)

Лист	Наименование	Примечание
31	План потолков	
32	Раскладка плитки. Планы полов	
33	Раскладка плитки. Прихожая. Коридор. Санузел. Ванная	
34	План полов	
35	Ведомость отделки помещений	
36	Колерная карта	
37	Спецификация отделочных материалов	
38	Спецификация отделочных материалов	
39	Концепция декора и визуализации	
40	План текстиля и декора	
41	Шторы и карнизы	
42	Ведомость текстиля	
43	Ведомость декора. Схемы развески	
44	Встроенная мебель. Схема расположения	
45	Система хранения Г1	
46	Шкаф-купе М11	
47	Система хранения Г2	
48	Шкаф распашной С5	
49	Кухня (пом. 3). Развёртка гарнитура	
50	Кухня (пом. 3). Монтажная схема	
51	Шкафы. Монтажная схема	
52	Ведомости изделий, техники и фурнитуры	
53	Реестр марок отделки и позиций альбома	

Общие указания — лист 4: ±0,000 — чистый пол; несущие конструкции и сети дома — по отдельному проекту; скрытые работы — по актам. Открытые вопросы и допущения — лист 5.

Изм.	Кол.уч	Лист	№ док.	Подп.	Дата
Разраб.		Кырпан А.С.			09.10.26
Пров.					
ГИП					
Н. контр.					
Утв.					

ГД-2026-007-АИ

Квартира 65 м²

Общая площадь 65,24* м² · * размеры со скана, не замерены (реестр — п. 5, К-1)

Дизайн-проект интерьера

Стадия	Лист	Листов
РП	2	79

Общие данные

М 6/м

Кырпан Александр Сергеевич

Общие данные

Комплект ГД-2026-007-АИ · лист 2 общих данных (продолжение)

Ведомость рабочих чертежей основного комплекта ГД-2026-007-АИ (продолжение)

Лист	Наименование	Примечание
54	Схема расположения развёрток и узлов	
55	Развёртки стен. Гардеробная (пом. 1)	
56	Развёртки стен А, Б. Спальня (пом. 2)	
57	Развёртки стен В, Г. Спальня (пом. 2)	
58	Развёртка стены В2. Кухня-гостиная (пом. 3), кухонный фронт	
59	Развёртка стены Г. Кухня-гостиная (пом. 3), кухонный фронт	
60	Развёртки стен А1, А2, Б1. Кухня-гостиная (пом. 3)	
61	Развёртки стен Б2, Б3, В1. Кухня-гостиная (пом. 3)	
62	Развёртки стен. Прихожая (пом. 4)	
63	Развёртки стен А, Б. Коридор (пом. 5)	
64	Развёртки стен В, Г. Коридор (пом. 5)	
65	Развёртки стен А, Б. Санузел (пом. 6)	
66	Развёртки стен В, Г. Санузел (пом. 6)	
67	Развёртки стен А, Б. Ванная (пом. 7)	
68	Развёртки стен В, Г. Ванная (пом. 7)	
69	Развёртки стен. Кладовая (пом. 8)	
70	Развёртки стен А, Б. Детская (пом. 9)	
71	Развёртки стен В, Г. Детская (пом. 9)	
72	Узлы	
73	Ведомость объёмов работ	
74	Ведомость объёмов работ (продолжение)	
75	Ведомость объёмов работ (окончание)	
76	Спецификация материалов	
77	Спецификация материалов (окончание)	
78	Смета ориентировочная	
79	Смета ориентировочная (окончание)	

Ведомость ссылочных и прилагаемых документов

Обозначение	Наименование	Примечание
	Ссылочные документы	
ГОСТ 21.201-2011	СПДС. Условные графические изображения элементов зданий, сооружений и конструкций	
ГОСТ 21.205-2016	СПДС. Условные обозначения элементов санитарно-технических систем	
ГОСТ 21.210-2014	СПДС. Изображения условные графические электрооборудования и проводок на планах	
ГОСТ 2.306-68	ЕСКД. Обозначения графические материалов и правила их нанесения на чертежах	
	Прилагаемые документы	
ГД-2026-007-АИ.В1	Визуализация. Вид сверху (3D): планировка с мебелью, текстилем и декором	альбом визуализаций
ГД-2026-007-АИ.В2	Визуализация. Интерьер: Ванная (пом. 7)	
ГД-2026-007-АИ.В3	Визуализация. Визуализация «room-bath-wB»	
ГД-2026-007-АИ.В4	Визуализация. Интерьер: Спальня (пом. 2)	
ГД-2026-007-АИ.В5	Визуализация. Визуализация «room-bedroom-wD»	
ГД-2026-007-АИ.В6	Визуализация. Визуализация «room-corridor-wA»	
ГД-2026-007-АИ.В7	Визуализация. Визуализация «room-corridor-wC»	
ГД-2026-007-АИ.В8	Визуализация. Интерьер: Прихожая (пом. 4)	
ГД-2026-007-АИ.В9	Визуализация. Визуализация «room-hall-wB»	
ГД-2026-007-АИ.В10	Визуализация. Интерьер: Детская (пом. 9)	
ГД-2026-007-АИ.В11	Визуализация. Визуализация «room-kids-wA»	
ГД-2026-007-АИ.В12	Визуализация. Визуализация «room-kids-wC»	
ГД-2026-007-АИ.В13	Визуализация. Визуализация «room-kids-wD»	
ГД-2026-007-АИ.В14	Визуализация. Интерьер: Кухня-гостиная (пом. 3)	
ГД-2026-007-АИ.В15	Визуализация. Интерьер: Кухня-гостиная (пом. 3)	
ГД-2026-007-АИ.В16	Визуализация. Визуализация «room-living-sofa»	

Допущения и предложения на листе

Основа листа: размеры сняты с растрового плана заказчика без размеров: масштаб восстановлен по площадям помещений (≈ 11,8 мм на пиксель), контрольный обмер не выполнен (К-1); высота потолка 2700 мм принята: на плане заказчика её нет (К-2); толщины стен 300 / 120 мм приняты по плану заказчика, не замерены (К-1); разрешённая мощность 15 кВт принята по типовым ТУ для квартиры, ТУ заказчиком не переданы (К-4).

См. лист открытых вопросов (лист 5, записи К-1, К-2, К-4).

Общие указания — лист 4: ±0,000 — чистый пол; несущие конструкции и сети дома — по отдельному проекту; скрытые работы — по актам. Открытые вопросы и допущения — лист 5.

Изм.	Кол.уч	Лист	№ док.	Подп.	Дата
Разраб.		Кырпан А.С.			09.10.26
Пров.					
ГИП					
Н. контр.					
Утв.					

ГД-2026-007-АИ

Квартира 65 м²

Общая площадь 65,24* м² · * размеры со скана, не замерены (реестр — л. 5, К-1)

Дизайн-проект интерьера

Стадия	Лист	Листов
РП	3	79

Общие данные

М 6/м

Кырпан Александр Сергеевич

выпуск 09.10.2026 № 147dabfd23 · стр. 5 из 110

Общие данные

Комплект ГД-2026-007-АИ · лист 3 общих данных (продолжение)

Ведомость ссылочных и прилагаемых документов (продолжение)

Обозначение	Наименование	Примечание
ГД-2026-007-АИ.В17	Визуализация. Визуализация «room-living-wB»	
ГД-2026-007-АИ.В18	Визуализация. Визуализация «room-wc-wC»	

Состав дизайн-проекта

Раздел	Состав	Листы
Обложка	Дизайн-проект интерьера; Квартира 65 м²; автор проекта — Кырпан Александр Сергеевич	1 с.
Концепция	Стиль Скандинавский: концепция интерьера, палитра и материалы (колерная карта лист 36)	л. 14
Визуализации	18 изобр.: Вид сверху (3D): планировка с мебелью, текстилем и декором; Ванная; Визуализация «room-bath-wB»; Спальня; Визуализация «room-bedroom-wD»; Визуализация «room-corridor-wA»; Визуализация «room-corridor-wC»; Прихожая; Визуализация «room-hall-wB»; Детская; Визуализация «room-kids-wA»; Визуализация «room-kids-wC»; Визуализация «room-kids-wD»; Кухня-гостиная; Кухня-гостиная; Визуализация «room-living-sofa»; Визуализация «room-living-wB»; Визуализация «room-wc-wC»	В1–В18
Рабочие чертежи	планы, развёртки, узлы (развёртки и узлы — листы 54–57, 60–72)	л. 1–79
Спецификации и ведомости	оборудование, изделия, отделка, электроточки	л. 13, 16, 17, 21, 29, 30, 35–38, 42, 43, 73–77

Условные обозначения

- контрольный отрезок 1000 мм натуры: по нему проверяют печать 1:1
- отметка уровня, м: ±0,000 — чистый пол жилых помещений
- (A) марка развёртки: буква стены, стрелка — взгляд
- (О1) марка отделки по реестру отделки альбома
- выноска узла: над полкой — узел, под полкой — лист

Общие указания

1. Рабочие чертежи интерьера разработаны на основании задания на проектирование и обмерного плана (лист 11). Объект: Квартира 65 м²; автор проекта — Кырпан Александр Сергеевич; общая площадь 65,24 м², жилая 43,2 м², помещений 9.
2. Рабочие чертежи выполнены в соответствии с заданием на проектирование и нормативными документами, перечисленными в п. 4.
3. Открытые вопросы, принятые допущения и конфликты между разделами, не снятые к выпуску комплекта, сведены в таблицы на листе 5. До ответа по пункту таблицы показанное на указанном там листе — допущение, а не утверждённое решение: комплект по этим листам предварительный.
4. Нормативные документы, на которые есть ссылки в листах комплекта: ГОСТ Р 21.101-2026; ГОСТ 21.501-2018; ГОСТ 2.302-68; ГОСТ 2.303-68; ГОСТ 2.304-81; ГОСТ 2.307-2011; СП 54.13330.2022; СП 71.13330.2017; СП 73.13330.2016; ПУЭ (7-е изд.), гл. 1.8, 7.1; ГОСТ Р 50571.7.701-2024; СанПиН 1.2.3685-21; ГОСТ 2.702; ГОСТ 2.755; ГОСТ 21.110-2013; ГОСТ 21.601; ГОСТ 13996-2019; ГОСТ 23166-2021; ГОСТ 31565-2012; ГОСТ 31975; ГОСТ 32414-2013; ГОСТ 32415-2013; ГОСТ Р 56387-2018; СП 29.13330.2011; СП 30.13330.2020; СП 51.13330.2011; СП 52.13330.2016. Документы из ведомости ссылочных документов здесь не повторяются.
5. За отметку ±0,000 принят уровень чистого пола жилых помещений квартиры (относительная отметка; абсолютная — по проекту дома). Отметка чистого пола мокрых помещений — −0,015. Размеры — в миллиметрах, отметки — в метрах, площади — в м²; высоты установки Н от чистого пола своего помещения до оси изделия.
6. Несущие конструкции, общедомовые стояки, вентиляционные каналы и инженерные сети дома настоящим комплектом не изменяются.
7. Трассы инженерных сетей на листах — принципиальные. Расчёты электрических нагрузок и токов КЗ, гидравлики, воздухообмена, освещённости и нагрузок на перекрытие выполняются в проектах ЭОМ, ВК, ОВ и КР организацией с допуском СРО; фактические трассы до закрытия отделкой фиксируются исполнительными схемами.
8. Стиль интерьера — Скандинавский. Палитра проекта: основной — NCS S 0500-N «S 0500-N»; дополнительный — NCS S 1500-N «S 1500-N», NCS S 2002-Y «S 2002-Y»; акцент — NCS S 4010-R90B «S 4010-R90B». Коды цвета — по веерам производителей; цвет утверждается по выкрасу на объекте при освещении проекта.
9. Площади поверхностей — по чистым граням стен до отделки: стены = периметр × высоту от чистого пола помещения до низа потолка минус проёмы (облицовка плиткой — до верха облицовки); плинтус = периметр минус дверные проёмы; пол и потолок — по площади помещения. Количество плиток — по раскладке. Способ один для всех листов комплекта (ведомость отделки, колерная карта, раскладка плитки, развёртки).
10. Марки: стены помещения на всех листах — А (верхняя по плану), Б (правая), В (нижняя), Г (левая); марка отделки О — одна на весь альбом; реестр марок отделки (с позициями колерной карты той же отделки) и марки позиций по видам — на листе 53.
11. Развёртки стен выполнены по всем помещениям для стен с электроточками, мебелью, декором и отделкой: санузлы и кухонный фронт — в М 1:25, остальные стены — в М 1:40; расположение развёрток и узлов — на листе 54, узлы — на листе 72.
12. Перечень скрытых работ, на которые составляются акты освидетельствования (форма по приказу Минстроя России № 344/пр): гидроизоляция пола и стен мокрых помещений (с тестом проливом); стяжка пола (толщина, прочность, влажность основания); тёплый пол до заливки (сопротивление, схема укладки); скрытая электропроводка (за потолком и в штробах стен; условия штробления — в следующем пункте); трубопроводы водоснабжения и канализации до закрытия (опрессовка, уклоны); закладные и усиления под подвесные приборы, мебель и тяжёлый декор, рамы инсталляций; короба дверей скрытого монтажа до штукатурки; каркасы ГКЛ потолков, коробов и перегородок до обшивки.
13. Скрытая электропроводка: за потолком и в штробах стен. Штробы в стенах выполняются только после технического заключения о несущих конструкциях; до заключения несущие стены не определены, и все стены считаются несущими; объём штроб — в ведомости объёмов работ, строка «Штробы в стенах» (вертикальные спуски; объём не меньше фактического, горизонтальные трассы — по исполнительной схеме).
14. Критерии приёмки: допуски отделочных покрытий — по СП 71.13330.2017; испытания систем водоснабжения и канализации — по СП 73.13330.2016 до закрытия трасс; приёмо-сдаточные испытания электроустановки — по ПУЭ, гл. 1.8, с протоколом электролаборатории.
15. Осознанные отступления от ГОСТ Р 21.101-2026, принятые в комплекте: номер листа и число листов («Листов») указаны на каждом листе; на масштабных листах в основной надписи указан фактический масштаб и дан контрольный отрезок 1000 мм; развёртки стен выполнены в М 1:25 и 1:40 (ГОСТ 21.507-81 — 1:50…1:500) ради читаемости привязок; размерные числа и марки элементов (Д-1, ОК-1, О6) — кеглем 2,5 мм, номера помещений — в кружке Ø 8 мм (канон — 3,5 мм и Ø 12 мм): так насыщенные листы А3 читаются без наложений надписей.
16. Графы «Пров.», «Н. контр.», «Утв.» основной надписи заполняются при согласовании комплекта с заказчиком; до согласования комплект подписывает автор проекта (графа «Разраб.»).

Допущения и предложения на листе

Основа листа: размеры сняты с растрового плана заказчика без размеров: масштаб восстановлен по площадям помещений (≈ 11,8 мм на пиксель), контрольный обмер не выполнен (К-1); высота потолка 2700 мм принята: на плане заказчика её нет (К-2); толщины стен 300 / 120 мм приняты по плану заказчика, не замерены (К-1); разрешённая мощность 15 кВт принята по типовым ТУ для квартиры, ТУ заказчиком не переданы (К-4).
См. лист открытых вопросов (лист 5, записи К-1, К-2, К-4).

Изм.	Кол.уч	Лист	№ док.	Подп.	Дата	ГД-2026-007-АИ			
						Квартира 65 м²			
						Общая площадь 65,24* м² · * размеры со скана, не замерены (реестр — п. 5, К-1)			
Разраб.		Кырпан А.С.			09.10.26	Дизайн-проект интерьера	Стадия	Лист	Листов
Пров.							РП	4	79
ГИП									
						Общие данные	Кырпан Александр Сергеевич		
Н. контр.						М 6/м			
Утв.									

выпуск 09.10.2026 № 147dabfd23 · стр. 6 из 110

Открытые вопросы, принятые допущения и конфликты

Сводка по реестрам координации (стартовое совещание 09.10.2026)

Комплект предварительный по пунктам этих таблиц. Пока по пункту нет ответа или решения, показанное на указанном листе — допущение проектировщика, а не утверждённое решение.
Сводка: открытых вопросов — 4 (из них ждут факта объекта — 1: контрольного обмера, обследования или документа).
Пункты, ответ на которые лежит на объекте, а не за столом проектировщика (графа «Вид», строка «Ждёт»), собраны на листе «Задание на контрольный обмер и обследование» (листы 6, 7): что и где замерить, с какой точностью и чем подтвердить. Пункты, ждущие решения человека, на объекте не закрываются.

Открытые вопросы и принятые допущения

№	Формулировка	Вид	Кто решает	Если решения нет	Лист, где это проявляется
К-1	Размеры квартиры сняты с растрового плана заказчика без размерных цепочек: масштаб восстановлен по подписанным площадям помещений. До заказа мебели, дверей и материалов нужен контрольный обмер всех помещений и проёмов.	Отсутствует Ждёт: обмера	Архитектор-планировщик	размеры на листах — по плану заказчика, уточняются по месту; мебель на заказ и материалы по ним не заказывать	л. 11 — Обмерный план л. 15 — План расстановки мебели
К-2	Высота потолка на плане заказчика не указана, принята 2700 мм.	Отсутствует	Архитектор-планировщик	высоты на развёртках и потолки — от 2700 мм, уточнить при обмере	л. 11 — Обмерный план л. 31 — План потолков
К-3	Спальня (пом. 2) по плану заказчика без окна: жилая комната должна иметь естественное освещение (СП 54.13330.2022). Нужно решение заказчика: перенести спальню к окну, дать окно или назначить помещение нежилым (гардеробная, кабинет).	Спорно	Архитектор-планировщик	помещение не может быть принято как жилая комната; планировка на согласование не подаётся	л. 11 — Обмерный план л. 15 — План расстановки мебели
К-4	Разрешённая мощность квартиры по ТУ неизвестна, принята 15 кВт.	Отсутствует	Инженер-электрик	щит и группы рассчитаны на 15 кВт; при меньших ТУ пересчёт	л. 22 — Однолинейная схема щита л. 18 — План розеток и электровыводов

Примечания

1. Номера листов — по ведомости рабочих чертежей комплекта (лист «Общие данные»).
2. Графа «Если решения нет» показывает состояние решения на листах; влияние на сроки и стоимость по пунктам не оценивалось.
3. Пункт, по которому принято решение, при следующем выпуске комплекта из таблиц исключается.

Изм.	Кол.уч	Лист	№ док.	Подп.	Дата	ГД-2026-007-АИ			
						Квартира 65 м²			
						Общая площадь 65,24* м² · * размеры со скана, не замерены (реестр — п. 5, К-1)			
Разраб.		Кырлан А.С.			09.10.26	Дизайн-проект интерьера	Стадия	Лист	Листов
Пров.							РП	5	79
ГИП									
						Открытые вопросы, принятые допущения и конфликты М б/м	Кырлан Александр Сергеевич		
Н. контр.									
Утв.									

Задание на контрольный обмер и обследование. Лист 1 из 2

Что замерить, вскрыть и получить до заказа материалов и изделий

Задание собрано из открытых вопросов, ответ на которые лежит на объекте или в документах, а не за столом проектировщика. Пока факт не получен, размер, материал или положение на листах — допущение (знак «*»), а не замер.
Сводка: на объекте — 7 (до демонтажа — 5; после демонтажа — 2); документом и при закупке — 1; из допущений в данных и на листах — 8, из них без вопроса в реестре — 5. Закрываются вопросы: К-1, К-2, К-4 (3). Вопросы, ждущие решения человека, задание не закрывает — они решаются по реестру открытых вопросов.

Условия проведения

Порядок работ	Приёмы и точность	Кто присутствует	Если факт не совпал с проектом
1. До демонтажа — существующее состояние: контур, диагонали, высоты, проёмы, оси стояков, ниши и конструкции, которые видны. 2. После демонтажа, до черновых работ — то, что закрывали отделка и короба: основание стен, фактические толщины, углы, узлы. 3. Документы и данные закупки — не на объекте: к сроку из последней таблицы, от них зависят привязки и заказ. Что заказывается по размеру из задания, до закрытия пункта не заказывают: сроки изготовления — по графику закупок прораба.	Обход по часовой стрелке от входа: стены, проёмы, потолок, коммуникации (стояки, щиток, вентканалы), особенности (ниши, короба, выступы). Размеры записывают в мм; сумма участков равна общему размеру, при цепочке длиннее трёх участков ставят проверочный (общий) размер. Диагонали каждого помещения; если две диагонали различаются на 5 мм и больше, разницу подписывают на плане. Потолок — в нескольких точках: центр, углы, у проёмов. Проём — ширина, высота, глубина откоса, привязка к ближайшим углам, высота подоконника. Допустимая погрешность прибора — 2–3 мм на метр; размеры округляют кратно 5 мм; два контрольных промера одного размера не должны расходиться более чем на 2 %. Допуск по пункту — в графе «Точность». План БТИ обмер не заменяет.	Прораб (отвечает за проведение) — назначает день и порядок обхода, открывает объект и освобождает помещения, ведёт это задание и реестр изменений. Архитектор — выполняет обмер, составляет акт контрольного обмера и подписывает результаты по размерам и конструкциям. Владельцы вопросов присутствуют при пунктах своего раздела или принимают результат до заказа: Инженер ВК (вода, канализация) позиции О-1; Инженер-электрик — К-4; позиции О-2; Инженер ОВ позиции О-3; Отделочник — позиции О-6, О-7. Заказчик или его представитель — передаёт документы (план БТИ, проект дома, технические условия, паспорта), подписывает акт. Проектных решений на обмере не принимают: обмер даёт факт, решения — по реестру открытых вопросов (лист 5).	1. В пределах допуска пункта — принимается измеренное значение, лист перевыпускается, знак «*» снимается. 2. Больше допуска или контрольные промеры расходятся более чем на 2 % — промер повторяют; не подтвердилось — запись в реестр изменений (дата, лист, было, стало, кто решил, подпись), работы в этом месте не начинают. 3. Затронуты несущая стена, стояк, вентканал или мокрая зона — сразу владельцу раздела и ГИПу (главному инженеру проекта); между разделами не больше двух кругов, затем решает ГИП. 4. На объекте устно ничего не согласуется: каждое решение — записью в реестр с подписью.

Этап 1. До демонтажа

№	Где	Способ	Что сделать	Кто выполняет	Точность	Что пересчитается в альбоме	Чем подтверждается	Закрывает вопросы реестра
О-1	Ввод В1 и Т3 у стояков; по всей квартире	Обмер	Отключающая арматура и счётчики воды на вводах: положение, тип, пломбы управляющей компании. Альбом ставит их на каждом вводе по практике, в данных их нет.	Архитектор	±5 мм	Узлы ввода в спецификации ВК (краны, фильтры, счётчики); места ввода на плане выводов. Листы: л. 27 — План выводов сантехники л. 29 — Спецификация сантехнического оборудования	акт контрольного обмера; фото с рулеткой и привязкой к стене или углу	Вопроса в реестре нет: Альбом принимает счётчики воды на вводах без осмотра. Результат принимает: Инженер ВК (вода, канализация)
О-2	Вход в квартиру или лестничная клетка; место щита на плане	Обмер	Существующий щиток и счётчик электроэнергии: место и габарит ниши, состояние ввода, марка и сечение вводного кабеля, наличие вводного автомата и УЗО, пломбы.	Архитектор	±5 мм	Ниша и место щита на листах; вводной кабель и аппараты на однолинейной схеме; расстояния до первых групп. Листы: л. 22 — Однолинейная схема щита	акт контрольного обмера; фото с рулеткой и привязкой к стене или углу	Вопроса в реестре нет: Альбом принимает щит и ввод без осмотра. Результат принимает: Инженер-электрик
О-3	у окон	Обмер	Положение стояков отопления (подающий и обратный) от граней стен, диаметры, наличие запорной арматуры; существующие радиаторы: число секций, межосевое расстояние, подводки. В данных стояков отопления нет — лист отопления выводит их условно у откоса окна.	Архитектор	±5 мм	План отопления: места стояков и подводок, привязки радиаторов; подбор радиаторов по теплотехническому расчёту; радиаторы и узлы подключения в ВОР и спецификации. Листы: л. 26 — План отопления	акт контрольного обмера; фото с рулеткой и привязкой к стене или углу	Вопроса в реестре нет: Альбом принимает положение стояков и радиаторов отопления без обмера. Результат принимает: Инженер ОВ
О-4	все помещения	Обмер	Контрольный обмер всех помещений: стороны, диагонали, проёмы, высота потолка.	исполнитель	±5 мм; диагонали — разница от 5 мм подписывается	обмерный и монтажный планы, развёртки, мебель на заказ Листы: л. 11 — Обмерный план л. 15 — План расстановки мебели	акт контрольного обмера	К-1 Результат принимает: Архитектор

Допущения и предложения на листе

Основа листа: размеры сняты с растрового плана заказчика без размеров: масштаб восстановлен по площадям помещений (≈ 11,8 мм на пиксель), контрольный обмер не выполнен (К-1); высота потолка 2700 мм принята: на плане заказчика её нет (К-2); толщины стен 300 / 120 мм приняты по плану заказчика, не замерены (К-1); разрешённая мощность 15 кВт принята по типовым ТУ для квартиры, ТУ заказчиком не переданы (К-4).
См. лист открытых вопросов (лист 5, записи К-1, К-2, К-4).

Изм.	Кол.уч	Лист	№ док.	Подп.	Дата	ГД-2026-007-АИ		
						Квартира 65 м²		
						Общая площадь 65,24* м² · * размеры со скана, не замерены (реестр — п. 5, К-1)		
Разраб.		Кырпан А.С.			09.10.26	Дизайн-проект интерьера	Стадия: РП	Лист: 6 / Листов: 79
Пров.								
ГИП						Задание на контрольный обмер и обследование. Лист 1 из 2 М б/м	Кырпан Александр Сергеевич	
Н. контр.								
Утв.								

выпуск 09.10.2026 № 147dabfd23 · стр. 8 из 110

Задание на контрольный обмер и обследование. Лист 2 из 2

Что замерить, вскрыть и получить до заказа материалов и изделий

Этап 1. До демонтажа (продолжение)

№	Где	Способ	Что сделать	Кто выполняет	Точность	Что пересчитается в альбоме	Чем подтверждается	Закрывает вопросы реестра
О-5	Все помещения квартиры	Обмер	Высота потолка в каждом помещении в нескольких точках: центр, углы, у проёмов.	Архитектор	±5 мм	Вертикальные размеры альбома: развёртки, шкафы, плитка, объёмы работ. Листы: л. 2–4 — Общие данные	акт контрольного обмера	К-2 Результат принимает: Архитектор

Этап 2. После демонтажа, до черновых работ

№	Где	Способ	Что сделать	Кто выполняет	Точность	Что пересчитается в альбоме	Чем подтверждается	Закрывает вопросы реестра
О-6	Гардеробная (пом. 1), Спальня (пом. 2), Кухня-гостиная (пом. 3), Прихожая (пом. 4), Коридор (пом. 5), Санузел (пом. 6), Ванная (пом. 7), Кладовая (пом. 8), Детская (пом. 9)	Обмер	Нивелировка плиты перекрытия и существующего пола после демонтажа покрытий: отметки в углах и по сетке, перепады по помещению, уклоны, отметки порогов (чистый пол в мокрых зонах принят -15 мм, 0 мм). Принятая толщина стяжки 50 мм и отметка чистого пола — расчётные, не от замера плиты.	Архитектор	±5 мм по отметке; ровность просвет под 2-метровой рейкой, горизонталь против 0,2 % длины помещения	Толщина стяжки и отметка чистого пола; уклоны к трапам и порогу; выпуски К1 относительно чистого пола (план разводки); объёмы стяжки и смеси в ВОР и спецификации. Листы: л. 32, 34 — План полов л. 28 — Схема разводки водопровода и канализации	акт контрольного обмера	Вопроса в реестре нет: Альбом принимает отметки плиты и толщину пирога пола без нивелировки. Результат принимает: Отделочник
О-7	Гардеробная (пом. 1), Спальня (пом. 2), Кухня-гостиная (пом. 3), Прихожая (пом. 4), Коридор (пом. 5), Санузел (пом. 6), Ванная (пом. 7), Кладовая (пом. 8), Детская (пом. 9)	Обмер	Вертикаль и плоскостность стен: отклонение от вертикали по высоте стены (отвес или лазерный уровень), просвет под правилом 2 м, кривизна углов. Нужно там, где от стены зависит изделие: облицовка плиткой (пом. 6, 7), штукатурка и окраска (пом. 1, 2, 3, 4, 5, 8, 9), встроенная мебель и кухня (пом. 3, 4, 9).	Архитектор	до 1 мм на 2 м (правило и клиновой щуп); вертикаль — мм на высоту стены, отклонения подписываются на плане	Толщина штукатурки и расход смеси в ВОР и спецификации; раскладка плитки (подрезка у стен); зазоры и крепление встроенной мебели и кухни. Листы: л. 32, 33 — Раскладка плитки л. 35 — Ведомость отделки помещений	акт контрольного обмера	Вопроса в реестре нет: Альбом принимает стены ровными и вертикальными без замера. Результат принимает: Отделочник

Документы и данные закупки (не на объекте)

№	У кого, откуда	Способ	Что получить	К какому сроку	Что пересчитается в альбоме	Чем подтверждается	Закрывает вопросы реестра
О-8	Заказчик; организация, выдавшая технические условия	Документ	Технические условия на присоединение: разрешённая мощность.	До утверждения однолинейной схемы щита	Однолинейная схема щита: вводной аппарат и группы. Листы: л. 2–4 — Общие данные	копия документа	К-4 Результат принимает: Инженер-электрик

Примечания

1. Подтверждение: акт контрольного обмера (дата, кто присутствовал, прибор, перечень промеров с результатами, подписи присутствующих); к акту — фото вскрытий и узлов и техническое заключение организации, выполнившей обследование.
2. Номера листов — по ведомости рабочих чертежей комплекта (лист «Общие данные»).
3. Пункт исключается из задания при следующем выпуске, когда акт подписан, значение внесено в проект и листы перевыпущены; знак «*» у величины снимается только замером.

Допущения и предложения на листе

Основа листа: размеры сняты с растрового плана заказчика без размеров: масштаб восстановлен по площадям помещений (≈ 11,8 мм на пиксель), контрольный обмер не выполнен (К-1); высота потолка 2700 мм принята: на плане заказчика её нет (К-2); толщины стен 300 / 120 мм приняты по плану заказчика, не замерены (К-1); разрешённая мощность 15 кВт принята по типовым ТУ для квартиры, ТУ заказчиком не переданы (К-4).

См. лист открытых вопросов (лист 5, записи К-1, К-2, К-4).

Изм.	Кол.уч	Лист	№ док.	Подп.	Дата			
Разраб.		Кырпан А.С.			09.10.26	ГД-2026-007-АИ		
Пров.						Квартира 65 м²		
ГИП						Общая площадь 65,24* м² · * размеры со скана, не замерены (реестр — п. 5, К-1)		
						Дизайн-проект интерьера	Стадия: РП	Лист: 7 / Листов: 79
Н. контр.						Задание на контрольный обмер и обследование. Лист 2 из 2 М 6\м	Кырпан Александр Сергеевич	
Утв.								

выпуск 09.10.2026 № 147dabfd23 · стр. 9 из 110

График закупок и работ. Лист 1 из 3

Что заказывать и когда не раньше чего: относительный порядок без дат; срок поставки — из данных или «уточняется у поставщика»

Лист не содержит дат: контрольного обмера, подписанных решений автора и договоров ещё нет, и любая дата была бы выдумана. Вместо календаря — порядок и условия: замер → решение и выбор изделия → заказ → срок поставки → работа, которую позиция блокирует.
Срок поставки печатается как срок, только если он задан в данных позиции. Нет — «срок уточняется у поставщика» и ссылка на вопрос реестра о сроках; типовой диапазон практики стоит рядом как ориентир и заказывать по нему нельзя. Номера З-N и Р-N — строки этого листа, К-N — записи реестра открытых вопросов, О-N — позиции задания на контрольный обмер.

Закупки: что заказывается, от чего зависит заказ и какую работу блокирует

№	Позиция и где	1. Замер до заказа	2. Решение, выбор изделия, паспорт	3. Условие заказа	4. Срок поставки	5. Блокирует работу	Закрывает вопросы реестра
З-1	Двери скрытого монтажа с коробом под покраску в существующих проёмах: Д-3, Д-2, Д-4 — 7 шт. пом. 1, 2, 5	О-4: обмер: все помещения (К-1); до заказа мебели и дверей		После 1 и 2 и после получения срока у поставщика (вопроса о сроках нет); дата заказа — когда срок известен, не позднее чем за срок до начала Р-6.	срок уточняется у поставщика Ориентир практики (не срок поставщика): ≈ 30 дн.	Р-6 «штукатурка»: короб ставят до штукатурки (коробку ставят на черновой стадии; полотно навешивают после чистовой отделки стен)	К-1
З-2	Кухонный гарнитур по проекту кухни: модули М4, М5, М6, М7, М8, М9 пом. 3			После 1 и 2 и после получения срока у поставщика (вопроса о сроках нет); дата заказа — когда срок известен, не позднее чем за срок до начала Р-16.	срок уточняется у поставщика Ориентир практики (не срок поставщика): 4–8 нед. от замера	Р-16 «кухня и мебель»: замер кухни — по готовым стенам после штукатурки или плитки, до чистового пола; производство идёт параллельно со стяжкой и отделкой	
З-3	Встраиваемая техника кухни: М8 холодильник пом. 3			После 1 и 2 и после получения срока у поставщика (вопроса о сроках нет); дата заказа — когда срок известен, не позднее чем за срок до начала Р-16.	срок уточняется у поставщика	Р-16 «кухня и мебель»: паспорта и монтажные схемы — до изготовления модулей кухни: нишу и вентзазоры задаёт модель, а не типовая схема 60 см	
З-4	Стиральная машина: П22 (вертикальная загрузка 400 × 600 мм — условие закупки) пом. 7			После 1 и 2 и после получения срока у поставщика (вопроса о сроках нет); дата заказа — когда срок известен, не позднее чем за срок до начала Р-5.	срок уточняется у поставщика	Р-5 «черновая сантехника»: габарит и подводка — до закрытия люка и разводки	
З-5	Сантехнические приборы и инсталляции: П4, П20, П21, П1, П3 пом. 3, 6, 7	О-3: обмер: у окон		После 1 и 2 и после получения срока у поставщика (вопроса о сроках нет); дата заказа — когда срок известен, не позднее чем за срок до начала Р-5.	срок уточняется у поставщика	Р-5 «черновая сантехника»: инсталляцию ставят до обшивки ГКЛВ и до гидроизоляции стены	
З-6	Керамогранит и плитка: 1 поз. по артикулу и формату, 15,34 м² по раскладке пом. 4, 5, 6, 7	О-6: обмер: Гардеробная (пом. 1), Спальня (пом. 2), Кухня-гостиная (пом. 3), Прихожая (пом. 4), Коридор (пом. 5), Санузел (пом. 6), Ванная (пом. 7), Кладовая (пом. 8), Детская (пом. 9) О-7: обмер: Гардеробная (пом. 1), Спальня (пом. 2), Кухня-гостиная (пом. 3), Прихожая (пом. 4), Коридор (пом. 5), Санузел (пом. 6), Ванная (пом. 7), Кладовая (пом. 8), Детская (пом. 9)		После 1 и 2 и после получения срока у поставщика (вопроса о сроках нет); дата заказа — когда срок известен, не позднее чем за срок до начала Р-10.	срок уточняется у поставщика	Р-10 «плитка»: калибр партии измеряют до раскладки, раскладку пересчитывают до заказа	
З-7	Покрытие пола (доска) и плинтус: пом. 1, 2, 3, 8, 9 пом. 1, 2, 3, 8, 9	О-6: обмер: Гардеробная (пом. 1), Спальня (пом. 2), Кухня-гостиная (пом. 3), Прихожая (пом. 4), Коридор (пом. 5), Санузел (пом. 6), Ванная (пом. 7), Кладовая (пом. 8), Детская (пом. 9)		После 1 и 2 и после получения срока у поставщика (вопроса о сроках нет); дата заказа — когда срок известен, не позднее чем за срок до начала Р-13.	срок уточняется у поставщика	Р-13 «чистовые полы»: артикул и партия — до заказа; доску привозят к чистовым полам	
З-8	Встроенная мебель по замеру цеха: М11, С5 пом. 4, 9	О-4: обмер: все помещения (К-1); до заказа мебели и дверей		После 1 и 2 и после получения срока у поставщика (вопроса о сроках нет); дата заказа — когда срок известен, не позднее чем за срок до начала Р-16.	срок уточняется у поставщика Ориентир практики (не срок поставщика): 4–8 нед. от замера	Р-16 «кухня и мебель»: цех замеряет по готовым стенам; производство 4–8 недель идёт параллельно с отделкой	К-1

Допущения и предложения на листе

Основа листа: размеры сняты с растрового плана заказчика без размеров: масштаб восстановлен по площадям помещений (≈ 11,8 мм на пиксель), контрольный обмер не выполнен (К-1); высота потолка 2700 мм принята: на плане заказчика её нет (К-2); толщины стен 300 / 120 мм приняты по плану заказчика, не замерены (К-1); разрешённая мощность 15 кВт принята по типовым ТУ для квартиры, ТУ заказчиком не переданы (К-4).
См. лист открытых вопросов (лист 5, записи К-1, К-2, К-4).

Изм.	Кол.уч	Лист	№ док.	Подп.	Дата
Разраб.		Кырпан А.С.			09.10.26
Пров.					
ГИП					
Н. контр.					
Утв.					

ГД-2026-007-АИ

Квартира 65 м²

Общая площадь 65,24* м² · * размеры со скана, не замерены (реестр — п. 5, К-1)

Дизайн-проект интерьера	Стадия	Лист	Листов
	РП	8	79
График закупок и работ. Лист 1 из 3 М 6/м	**Кырпан Александр Сергеевич**		

выпуск 09.10.2026 № 147dabfd23 · стр. 10 из 110

График закупок и работ. Лист 2 из 3

Что заказывать и когда не раньше чего: относительный порядок без дат; срок поставки — из данных или «уточняется у поставщика»

Работы: порядок и что не даёт начать

№	Работа (стадия технологической последовательности)	После	Что должно быть к началу: условия и закупки	Не начинать, пока открыто в реестре
Р-1	Демонтаж покрытий, отделки стен и потолков, дверных блоков и приборов; конструкции, стены и перегородки не трогать до технического заключения (стадия 1)		до начала: запрошены документы на дом и БТИ; контрольный обмер до демонтажа (что видно) сделан	
Р-2	Контрольный обмер на голых стенах и обследование (задание — лист «Задание на контрольный обмер») (стадия 2)	Р-1	после снятия отделки: видны стояки, каналы, щиток, толщины стен; до заказа всего, что делают по размеру	
Р-3	Перегородки и фальш-стены ГКЛ: разметка, каркас, обшивка (стадия 3)	Р-2	до начала: решение по нише санузла 2 принято автором; разметка по плану монтажа подписана; коробка скрытой двери — в каркас до обшивки	К-1: Размеры квартиры сняты с растрового плана заказчика без размерных цепочек: масштаб восстановлен по подписанным площадям помещений.
Р-4	Черновая электрика: штробы, короба, гофра, подрозетники, щит (стадия 4)	Р-2, Р-3	до начала: план электрики с высотами утверждён; штробы в стенах — только после технического заключения; мебель расставлена	К-4: Разрешённая мощность квартиры по ТУ неизвестна, принята 15 кВт.
Р-5	Черновая сантехника и вентиляция: разводка, выводы, инсталляции, короба стояков (стадия 5)	Р-2, Р-3	до начала: положение стояков замерено; модели инсталляций и машины выбраны (габариты рамы, подводка); инсталляцию ставят до обшивки ГКЛВ и до гидроизоляции Закупки к началу: З-4 (стиральная машина), З-5 (сантехника)	
Р-6	Коробки скрытых дверей, затем штукатурка стен и откосов (стадия 6)	Р-3, Р-4, Р-5	до начала: электрика и сантехника смонтированы, штробы заделаны; коробки скрытых дверей установлены до штукатурки (поэтому заказ дверей — раньше работы) Закупки к началу: З-1 (двери скрытого монтажа)	К-1: Размеры квартиры сняты с растрового плана заказчика без размерных цепочек: масштаб восстановлен по подписанным площадям помещений.
Р-7	Стяжка пола и тёплый пол (стадия 7)	Р-6	до начала: штукатурка сделана; трубы под стяжкой приняты; нивелировка плиты выполнена	
Р-8	Гидроизоляция санузлов и тест проливом (стадия 8)	Р-7	до начала: стяжка набрала прочность и сухая по инструкции гидроизоляции; выводы стоят на проектных отметках	
Р-9	ГКЛ: короба инсталляции и стояков, ниши, потолки (стадия 9)	Р-4, Р-5	до начала: черновые сети в зоне коробов приняты; закладные под тюлевое и карнизы стоят; светильники выбраны (вырезы)	
Р-10	Плитка и керамогранит: стены, затем пол; фартук (стадия 10)	Р-7, Р-8, Р-9	до начала: гидроизоляция принята; плитка выбрана, калибр партии измерен, раскладка пересчитана и подписана Закупки к началу: З-6 (плитка)	
Р-11	Шпаклёвка стен и потолков под окраску (стадия 11)	Р-6, Р-9, Р-10	до начала: плитка готова (грязные работы закончены); штукатурка и ГКЛ сухие	
Р-12	Окраска стен, потолков, откосов (стадия 13)	Р-11	до начала: шпаклёвка отшлифована и огрунтована; выкрасы утверждены, колеровка одной партией	
Р-13	Чистовые полы: инженерная доска (стадия 14)	Р-10, Р-12	до начала: влажность основания в норме, мокрые работы закончены; доска выбрана и привезена Закупки к началу: З-7 (доска и плинтус)	
Р-14	Полотна межкомнатных дверей, плинтусы, пороги (стадия 15)	Р-12, Р-13	до начала: чистовой пол уложен; полотна скрытых дверей — после чистовой отделки стен	
Р-15	Чистовая электрика и сантехника: механизмы, светильники, смесители, приборы (стадия 16)	Р-12, Р-14	до начала: отделка готова; механизмы, светильники и приборы выбраны и привезены	
Р-16	Кухня, встроенная и корпусная мебель, бытовая техника (стадия 17)	Р-14, Р-15	до начала: чистовая сантехника и электрика подведены к местам мебели; замер кухни снят по готовым стенам (после штукатурки или плитки, до чистового пола) Закупки к началу: З-2 (кухонный гарнитур), З-3 (техника кухни), З-8 (мебель по замеру)	К-1: Размеры квартиры сняты с растрового плана заказчика без размерных цепочек: масштаб восстановлен по подписанным площадям помещений.
Р-17	Сдача: осмотр по чек-листу, дефектная ведомость, устранение замечаний (стадия 18)	Р-15, Р-16	до начала: всё смонтировано; акты скрытых работ подписаны	

Допущения и предложения на листе

Основа листа: размеры сняты с растрового плана заказчика без размеров: масштаб восстановлен по площадям помещений (≈ 11,8 мм на пиксель), контрольный обмер не выполнен (К-1); высота потолка 2700 мм принята: на плане заказчика её нет (К-2); толщины стен 300 / 120 мм приняты по плану заказчика, не замерены (К-1); разрешённая мощность 15 кВт принята по типовым ТУ для квартиры, ТУ заказчиком не переданы (К-4).

См. лист открытых вопросов (лист 5, записи К-1, К-2, К-4).

Изм.	Кол.уч	Лист	№ док.	Подп.	Дата	ГД-2026-007-АИ			
						Квартира 65 м²			
						Общая площадь 65,24* м² · * размеры со скана, не замерены (реестр — п. 5, К-1)			
Разраб.		Кырпан А.С.			09.10.26	Дизайн-проект интерьера	Стадия	Лист	Листов
Пров.							РП	9	79
ГИП									
						График закупок и работ. Лист 2 из 3	Кырпан Александр Сергеевич		
Н. контр.						М 6/м			
Утв.									

выпуск 09.10.2026 № 147dabfd23 · стр. 11 из 110

ПРЕДВАРИТЕЛЬНО · не для производства работ · открыто пунктов: 4 (реестр — л. 5)

График закупок и работ. Лист 3 из 3

Что заказывать и когда не раньше чего: относительный порядок без дат; срок поставки — из данных или «уточняется у поставщика»

Примечания

1. Порядок работ — стадии технологической последовательности из 17 позиций, присутствующих в этом проекте (по строкам ведомости объёмов); остальные стадии таблицы knowledge/remont-tehnologiya.md в проекте не встречаются. Длительности работ не печатаются: их нет ни в данных, ни в нормах для этого объекта.
2. Типовые сроки — ориентир практики, не срок поставщика: скрытые двери — короб около 10 дн., полотно под покраску до 3 нед., шпон 4–5 нед., в среднем около 30 дн. (knowledge/workers/foreman.md, п. 2.4 (profil-doors)); кухня и корпусная мебель — 4–8 недель от замера (knowledge/remont-tehnologiya.md, разд. 2; knowledge/workers/foreman.md, п. 2.4). Заказ по ориентиру не назначается: срок получают у поставщика (вопрос реестра), после чего заказ планируют «не позднее чем за срок до начала работы».
3. Условия заказа берутся из реестра открытых вопросов и задания на контрольный обмер: позиция заказывается, когда закрыты замер (графа 1) и решение (графа 2). Закрывать их может только факт или решение автора с подписью; снять строку с листа можно только закрыв запись реестра.
4. Заказ по размеру до контрольного обмера не делают: двери, кухня и встроенная мебель зависят от обмера (К-11, К-13); скрытые двери, кроме того, зависят от решения по нише санузла 2 (проём Д-5 в перегородке П-1).
5. Номера листов — по ведомости рабочих чертежей комплекта (лист «Общие данные»).

Допущения и предложения на листе

Основа листа: размеры сняты с растрового плана заказчика без размеров: масштаб восстановлен по площадям помещений (≈ 11,8 мм на пиксель), контрольный обмер не выполнен (К-1); высота потолка 2700 мм принята: на плане заказчика её нет (К-2); толщины стен 300 / 120 мм приняты по плану заказчика, не замерены (К-1); разрешённая мощность 15 кВт принята по типовым ТУ для квартиры, ТУ заказчиком не переданы (К-4).
См. лист открытых вопросов (лист 5, записи К-1, К-2, К-4).

						ГД-2026-007-АИ
						Квартира 65 м²
						Общая площадь 65,24* м² · * размеры со скана, не замерены (реестр — п. 5, К-1)
Изм.	Кол.уч	Лист	№ док.	Подп.	Дата	
Разраб.		Кырпан А.С.			09.10.26	Дизайн-проект интерьера — Стадия: РП; Лист: 10; Листов: 79
Пров.						
ГИП						
						График закупок и работ. Лист 3 из 3 — М 6/м
Н. контр.						**Кырпан Александр Сергеевич**
Утв.						

01

Архитектурные решения

Кырлан Александр Сергеевич

выпуск 09.10.2026 № 147dabfd23 · стр. 13 из 110

Обмерный план

Существующее положение · размеры в мм · отметки от чистого пола

ПРЕДВАРИТЕЛЬНО · не для производства работ · открыто пунктов: 4 (реестр — л. 5)


Отметки по высоте

±0,000	чистый пол пом. 1–5, 8, 9; отсчёт высот
−0,015	чистый пол пом. 6, 7, ниже на 15 мм
−0,064*	верх плиты — расчёт, не замер (задание на обмер)
сущ. пол	снимается до плиты; не замерен (задание на обмер)

Принято, не определено или спорно

полностью — лист 5

К-3 — Спальня (пом. 2) по плану заказчика без окна: жилая комната должна иметь естественное освещение (СП 54.13330.2022)

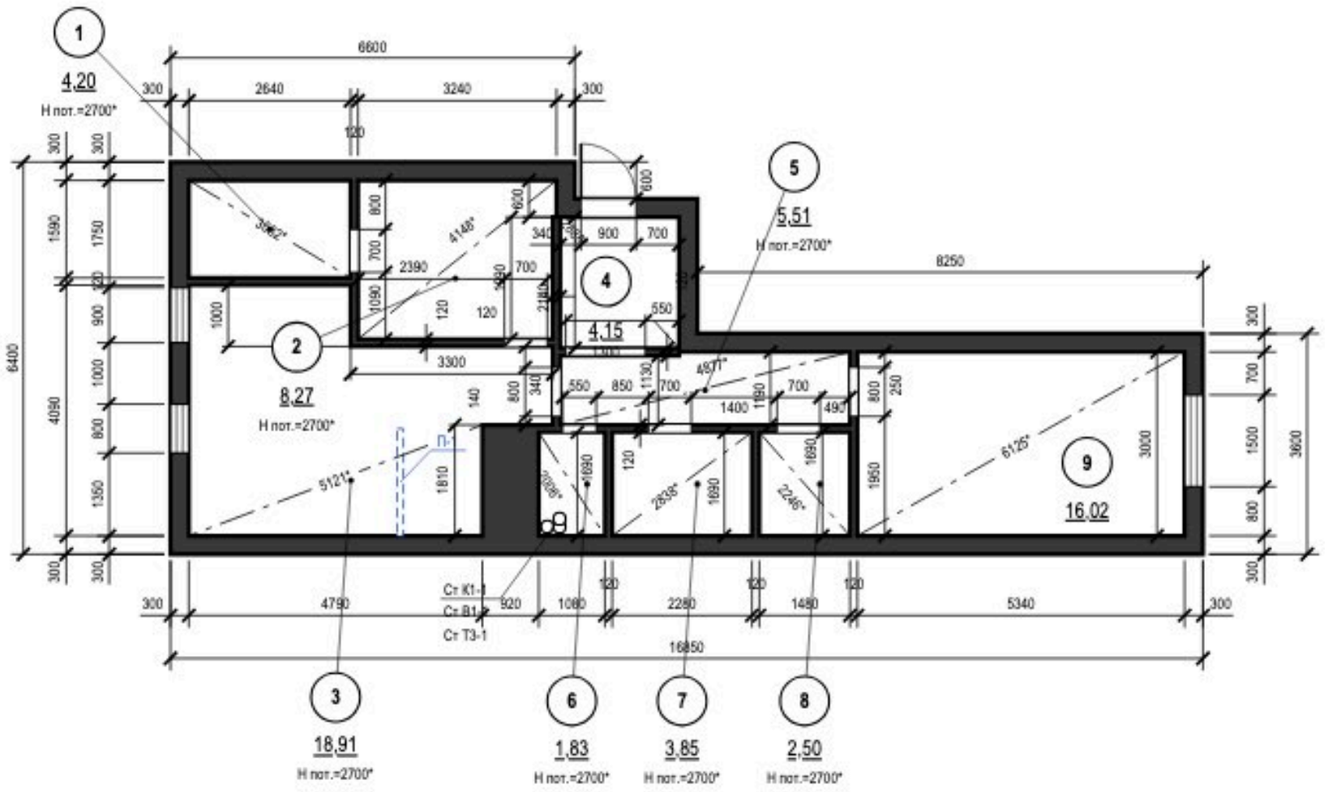

Экспликация помещений

№	Наименование	Площадь, м²
1	Гардеробная	4,20
2	Спальня	8,27
3	Кухня-гостиная	18,91
4	Прихожая	4,15
5	Коридор	5,51
6	Санузел	1,83
7	Ванная	3,85
8	Кладовая	2,50
9	Детская	16,02
	Итого (общая площадь)	**65,24**

Условные обозначения

- существующие стены (сечение)
- окно (рама, остекление)
- проём существующий, без заполнения (откосы)
- стояк К1 — канализация, В1 — ХВС, Т3 — ГВС
- проектная конструкция — на объекте её нет (контур)
- диагональ помещения — контроль прямоугольности
- (1) номер помещения, площадь м²

Примечания

1. Размеры — в мм по чистым поверхностям стен до отделки (по плану заказчика); площади — в м² по тем же размерам. До начала работ выполнить контрольный обмер.
2. Источник плана — допущение, не замер: растровый скан плана заказчика, размеры сняты с размерных цепочек, на объекте не замерены. Реестр: лист 5, вопрос К-1.
3. За отметку ±0,000 принят чистый пол, не существующий (блок отметок). Н пот. — высота от чистого пола до плиты перекрытия; Н пот. со знаком «*» — принятая высота, не замер (вопрос К-2).
4. Толщины стен: наружные 300 мм, перегородки 120 мм; отличающиеся толщины и уступы размерами на плане.
5. Несущие стены не определены: до технического заключения все стены считать несущими; проёмы и штробы в них не выполнять.
6. Дверные проёмы показаны без заполнения (двери — лист 13); высота дверных проёмов 2100 мм, проёмов без двери 2100 мм; низ окон (подоконник) 800 мм от чистого пола, высота окон 1600 мм.
7. Диагонали — контрольные размеры; «*» — расчёт по принятому контуру (К-1), при обмере заменить замеренным; расхождение более 5 мм подписать на плане как перекос.
8. Размеры проверить на месте до начала работ; расхождение контрольных промеров ≤ 2 %.
9. Размеры короче 1 мм на листе цепочкой не показаны (две выносные линии на таком расстоянии сливаются): пом. 2, стена В — 90 мм от проёма до угла; пом. 4, стена В — 90 мм от угла до проёма; пом. 5, стена В — 40 мм от угла до проёма.

Допущения и предложения на листе

Основа листа: размеры сняты с растрового плана заказчика без размеров: масштаб восстановлен по площадям помещений (≈ 11,8 мм на пиксель), контрольный обмер не выполнен (К-1); высота потолка 2700 мм принята: на плане заказчика её нет (К-2); толщины стен 300 / 120 мм приняты по плану заказчика, не замерены (К-1); разрешённая мощность 15 кВт принята по типовым ТУ для квартиры, ТУ заказчиком не переданы (К-4).

Открытые вопросы и конфликты по листу: К-1–К-3.

См. лист открытых вопросов (лист 5, записи К-1–К-4).

1000 мм · печать 1:1

Изм.	Кол.уч	Лист	№ док.	Подп.	Дата
Разраб.		Кырпан А.С.			09.10.26
Пров.					
ГИП					
Н. контр.					
Утв.					

ГД-2026-007-АИ

Квартира 65 м²

Общая площадь 65,24* м² · * размеры со скана, не замерены (реестр — п. 5, К-1)

Дизайн-проект интерьера

Стадия	Лист	Листов
РП	11	79

Обмерный план

М 1:100


Кырпан Александр Сергеевич

выпуск 09.10.2026 № 147dabfd23 · стр. 14 из 110

План демонтажа и монтажа перегородок

Существующее — серым, демонтаж — красным, монтаж — синим · размеры в мм

ПРЕДВАРИТЕЛЬНО · не для производства работ · открыто пунктов: 4 (реестр — л. 5)

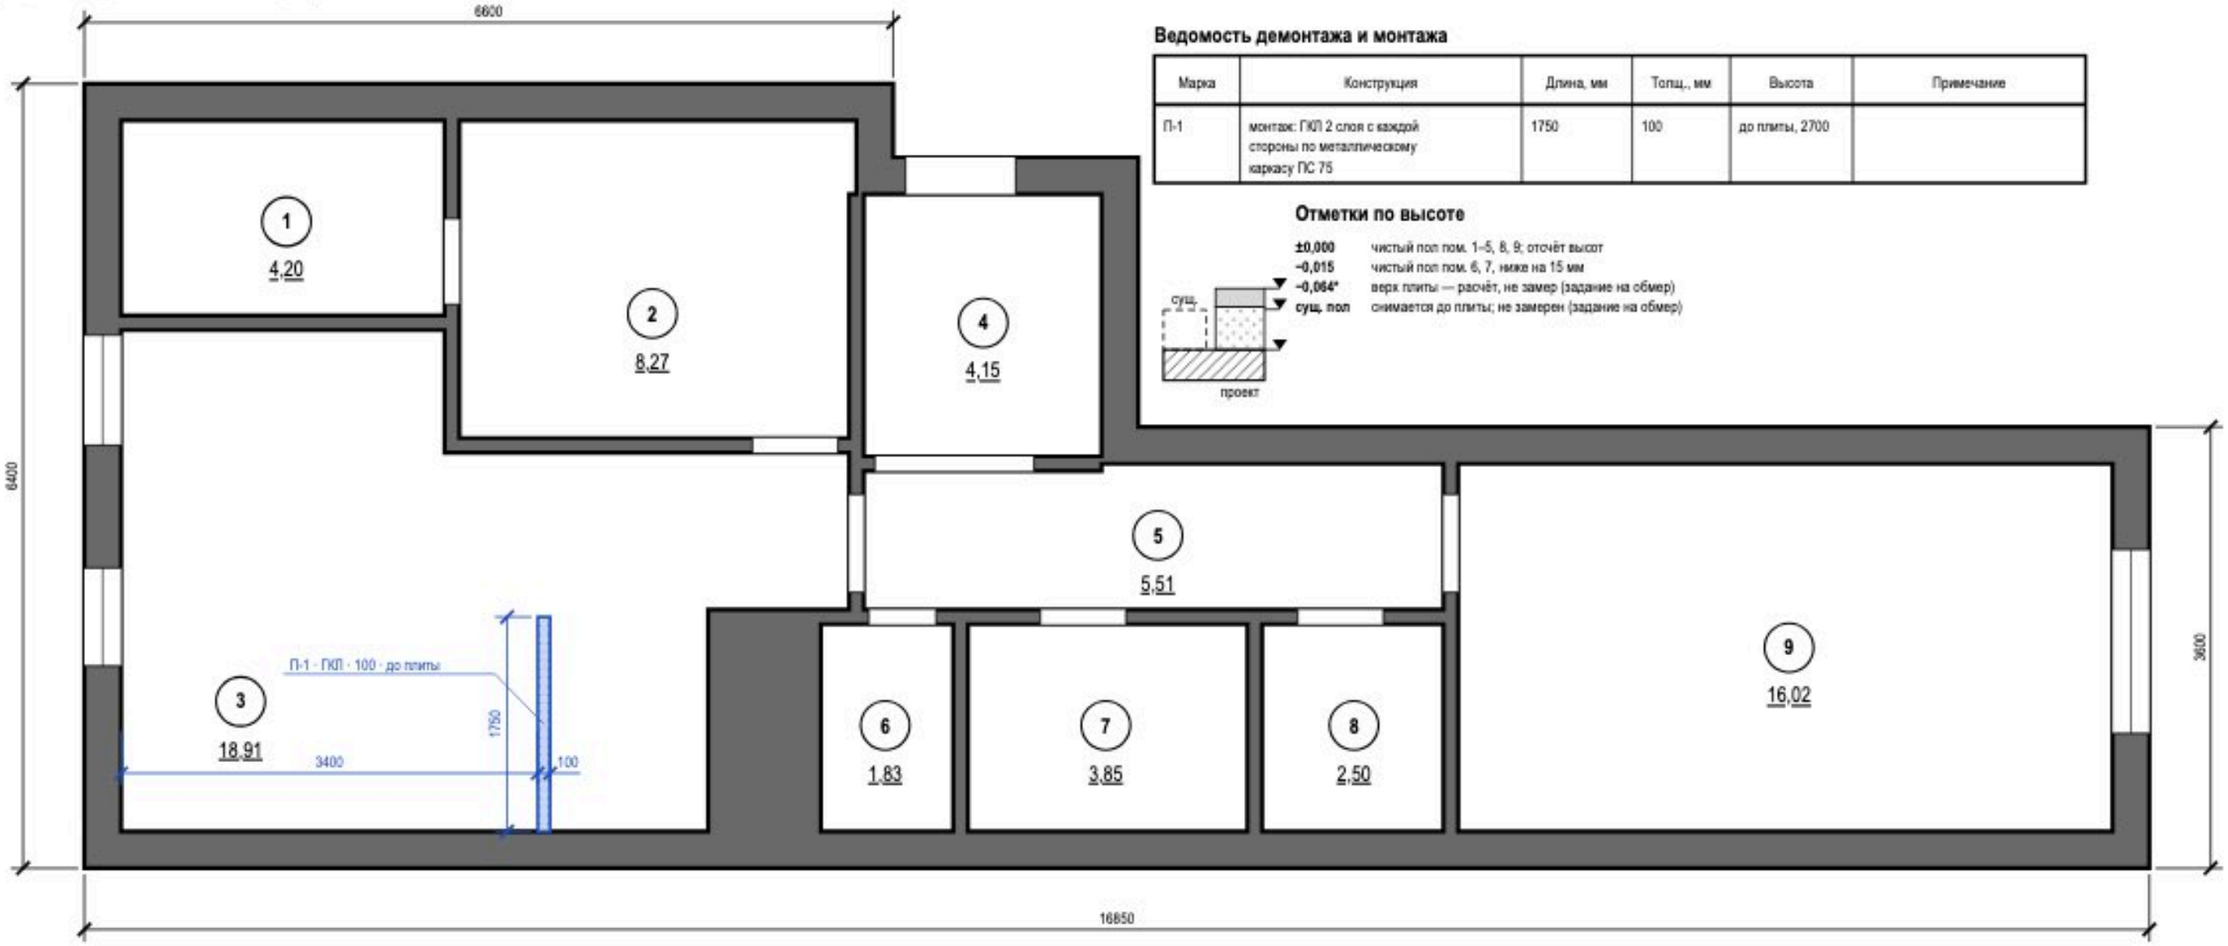

Ведомость демонтажа и монтажа

Марка	Конструкция	Длина, мм	Толщ., мм	Высота	Примечание
П-1	монтаж: ГКЛ 2 слоя с каждой стороны по металлическому каркасу ПС 75	1750	100	до плиты, 2700	

Отметки по высоте

±0,000	чистый пол пом. 1–5, 8, 9; отсчёт высот
−0,015	чистый пол пом. 6, 7, ниже на 15 мм
−0,064*	верх плиты — расчёт, не замер (задание на обмер)
сущ. пол	снимается до плиты; не замерен (задание на обмер)

Условные обозначения

- существующие стены — сохраняются;
- несущие не определены — считать несущими
- демонтируемые конструкции — на плане нет
- новое — возводится по проекту (синим)
- проём существующий, без заполнения (откосы)
- (1) номер помещения, площадь м²

Примечания

1. Демонтаж несущих стен и плит перекрытия не производится.
2. Новые перегородки и фальш-стены (синим) привязаны от капитальных стен и наружного контура; высота — по ведомости («до плиты» — до низа плиты перекрытия); проёмы в них усилить стойками каркаса.
3. Перепланировку согласовать до начала работ (ЖК РФ, ст. 26); план не передавать в работу до допуска главного инженера проекта.
4. Дверные блоки — по плану дверей (лист 13); существующие проёмы не расширяются.
5. Демонтаж существующих покрытий пола, стен и потолка, дверных блоков и сантехприборов (если есть) — до основания; объёмы демонтажа — для справки, по факту на объекте.
6. За отметку ±0,000 принят чистый пол, не существующий (блок отметок). Размеры — в мм по чистовой поверхности стен до отделки.
7. Размеры проверить на месте до начала работ: расхождение с обмером — не более 2 % (иначе — к архитектору).
8. Несущие стены не определены: до технического заключения все стены считать несущими — проёмы, ниши и штробы в них не выполнять.

Допущения и предложения на листе

Основа листа: размеры сняты с растрового плана заказчика без размеров: масштаб восстановлен по площадям помещений (≈ 11,8 мм на пиксель), контрольный обмер не выполнен (К-1); высота потолка 2700 мм принята: на плане заказчика её нет (К-2); толщины стен 300 / 120 мм приняты по плану заказчика, не замерены (К-1); разрешённая мощность 15 кВт принята по типовым ТУ для квартиры, ТУ заказчиком не переданы (К-4).

См. лист открытых вопросов (лист 5, записи К-1, К-2, К-4).

1000 мм · печать 1:1

Изм.	Кол.уч	Лист	№ док.	Подп.	Дата
Разраб.		Кырпан А.С.			09.10.26
Пров.					
ГИП					
Н. контр.					
Утв.					

ГД-2026-007-АИ

Квартира 65 м²

Общая площадь 65,24* м² · * размеры со скана, не замерены (реестр — п. 5, К-1)

Дизайн-проект интерьера	Стадия	Лист	Листов
	РП	12	79

План демонтажа и монтажа перегородок

М 1:50


Кырпан Александр Сергеевич

выпуск 09.10.2026 · 147dabfd23 · стр. 15 из 110

План дверей и ведомость заполнения проёмов

Проёмы, марки заполнения, привязки · размеры в мм

ПРЕДВАРИТЕЛЬНО · не для производства работ · открыто пунктов: 4 (реестр — л. 5)

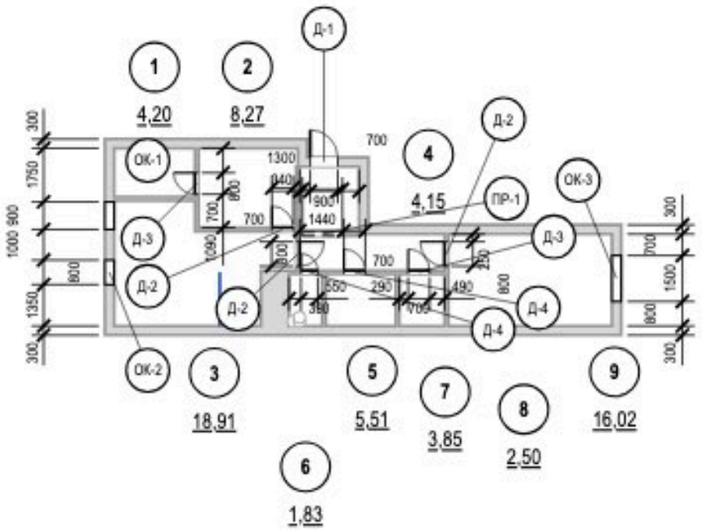

Ведомость заполнения проёмов

Марка	Наименование, обозначение	Проём ш×в, мм	Кол.	Откр.	Отделка полотна	Фурнитура	Прим.
Д-1	Блок дверной входной, ГОСТ 31173-2016	900×2100	1	П	в комплекте блока	в комплекте блока (замки, глазок)	наружу
Д-2	Дверь скрытого монтажа, ТУ изготовителя	700×2100	3	П, П, Л	S 1502-Y50R — пом. 2, S 1002-Y50R — пом. 3; S 1502-Y50R — пом. 5, S 1002-Y50R — пом. 3; S 1502-Y50R — пом. 5, No. 241 — пом. 9	скрытые петли 3D, магнитный замок	
Д-3	Дверь скрытого монтажа, ТУ изготовителя	700×2100	2	Л, П	V503 — пом. 1, S 1502-Y50R — пом. 2; S 1502-Y50R пом. 5, S 0502-Y — пом. 8	скрытые петли 3D, магнитный замок	
Д-4	Дверь скрытого монтажа, ТУ изготовителя	550×2100	2	П, П	S 1502-Y50R — пом. 5, в тон облицовки — пом. 6; S 1502-Y50R — пом. 5, в тон облицовки — пом. 7	скрытые петли 3D, магнитный замок, фиксатор WC	порог 15
ПР-1	Портал без заполнения	1300×2100	1				6in
ОК-1	Блок оконный, ГОСТ 23166-2021	900×1600	1				низ 800
ОК-2	Блок оконный, ГОСТ 23166-2021	800×1600	1				низ 800
ОК-3	Блок оконный, ГОСТ 23166-2021	1500×1600	1				низ 800

Условные обозначения

- стены (подложка обмера)
- новое — возводится по проекту (синим)
- дверь распашная, дуга открывания
- дверь скрытого монтажа
- дверь входная (полотно толще)
- портал (штрих — перемычка)
- оконный блок
- Д — марка типа (Д-N, ПР-N, ОК-N)
- 1 — номер помещения, площадь м²

Примечания

1. Размеры проёмов и привязки — в миллиметрах от чистых граней стен до отделки; привязка — от угла того помещения, со стороны которого стоит размер. Размер в ведомости — ширина × высота проёма от чистого пола 0,000. Откос от угла помещения до проёма с коробкой — не менее 50 мм.
2. Марки в кружках — типы заполнения проёмов (ГОСТ 21.501-2018, п. 5.3.2); одна марка — один типоразмер; количество сверено с планом.
3. Открывание: Л — петли слева, П — справа, если смотреть со стороны, куда открывается полотно (на себя).
4. Скрытые двери (Д-2…Д-4): проём замерить в чистоте; блок заказать до штукатурки (≈ 30 дн.), короб ставить до штукатурки; полотно навесить после чистовой отделки, красить в цвет стен. Порядок практика монтажа, изготовитель подтверждает.
5. Размер в ведомости — проёма: полотно скрытой двери уже проёма на коробку и зазор 10–15 мм (модель не выбрана); Д-2…Д-4 — существующие проёмы, до техзаключения не расширять.
6. Д-1: дуга наружу — по плану заказчика, не проверено; блок оставить или заменить — не решено.
7. Размеры проёмов и привязки сняты со скана плана заказчика и на объекте не замерены (обмерный план — лист 11).
8. Экспликация помещений — лист 11; в марках помещений — номер и площадь, м².
9. Марки Д-2, Д-4: разные типоразмеры под одной маркой — развести марки.
10. Привязка проёма к углу помещения меньше 1 мм на листе, размер на плане не показан: Д-2 — 90 мм; ПР-1 — 90 мм; Д-2 — 140 мм; Д-4 — 140 мм.

Допущения и предложения на листе

Основа листа: размеры сняты с растрового плана заказчика без размеров: масштаб восстановлен по площадям помещений (≈ 11,8 мм на пиксель), контрольный обмер не выполнен (К-1); высота потолка 2700 мм принята: на плане заказчика её нет (К-2); толщины стен 300 / 120 мм приняты по плану заказчика, не замерены (К-1); разрешённая мощность 15 кВт принята по типовым ТУ для квартиры, ТУ заказчиком не переданы (К-4).

См. лист открытых вопросов (лист 5, записи К-1, К-2, К-4).

1000 мм · печать 1:1

Изм.	Кол.уч	Лист	№ док.	Подп.	Дата
Разраб.		Кырпан А.С.			09.10.26
Пров.					
ГИП					
Н. контр.					
Утв.					

ГД-2026-007-АИ

Квартира 65 м²

Общая площадь 65,24* м² · * размеры со скана, не замерены (реестр — л. 5, К-1)

Дизайн-проект интерьера	Стадия	Лист	Листов
	РП	13	79

План дверей и ведомость заполнения проёмов

М 1:200

Кырпан Александр Сергеевич

выпуск 09.10.2026 № 147dabfd23 · стр. 16 из 110

02

Планировочное решение

Кырлан Александр Сергеевич

выпуск 09.10.2026 № 147dabfd23 - стр. 17 из 110

Концепция интерьера

Скандинавский · схема нейтральная · 60/30/10 · материалы, образы и зонирование

Идея

Стиль — скандинавский: светло, спокойно, уютно (hygge), естественно, функционально, в меру (lagom). Тёплые нейтрали NCS (стены по ведомости — S 1002-Y50R / S 1502-Y50R близки к ним), акцент — пыльный синий в текстиле. Цветовая схема — нейтральная, пропорция 60/30/10: база на стенах и потолках, вторичный цвет — в текстиле и мягкой мебели, акцент — точечно.

Мудборд: материалы и фактуры



IM1848
пол




SG501600R
пол



NCS S 0300-N
потолок, плинтус



NCS S 1502-Y50R
стены

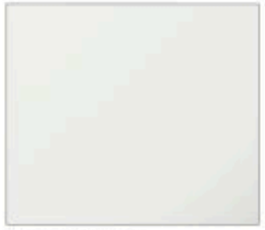

Winter · Tikkurila V503
стены, потолок, плинтус



NCS S 1002-Y50R
стены



NCS S 0502-Y
стены



Skimming Stone · Farrow & Ball No. 241
стены, плинтус



Hague Blue · Farrow & Ball No. 30
акцент (стена А)

Палитра 60/30/10

60 %	30 %	10 %

60 % база — NCS S 0500-N, LRV 85


30 % вторичный — NCS S 1500-N, LRV 64; NCS S 2002-Y, LRV 55

10 % акцент — NCS S 4010-R90B, LRV 27

Свет

Цветовая температура 2700–4000 K (диапазон стиля 2700–3000 K); CRI не ниже 90; сценарии: вечер. Общий свет — споты с диммированием, акцент — скрытая линейная подсветка, у кроватей — бра.

Функциональное зонирование (М 1:200)

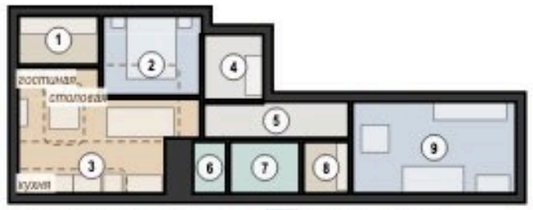

- дневная зона: гостиная, кухня, столовая
- ночная зона: спальни
- мокрая зона: санузлы
- хранение: гардеробная, кладовая
- вход и коммуникации
- функциональная зона в помещении
- (1) номер помещения (лист 15)

Образы помещений

3. Кухня-гостиная — 18,91 м²
стены NCS S 1002-Y50R
пол — IM1848
свет 3000/4000 K

2. Спальня — 8,27 м²
стены NCS S 1502-Y50R
пол — IM1848
свет 2700 K

9. Детская — 16,02 м²
стены Farrow & Ball No. 241; акцент No. 30 на стене А
пол — IM1848
текстиль: портьеры H487, тюль V503, ковёр V484

4. Прихожая — 4,15 м²
стены NCS S 1502-Y50R
пол — SG501600R
свет 3000 K

5. Коридор — 5,51 м²
стены NCS S 1502-Y50R
пол — SG501600R
свет 3000 K

1. Гардеробная — 4,20 м²
стены Tikkurila V503
пол — IM1848
свет 3000 K

7. Ванная — 3,85 м²
стены Italon 610010001195
пол — SG501600R
свет 3000 K

6. Санузел — 1,83 м²
стены Italon 610010001195
пол — SG501600R
свет 3000 K

8. Кладовая — 2,50 м²
стены NCS S 0502-Y
пол — IM1848
свет 3000 K

Материалы и отделка

IM1848
пол — пом. 1, 2, 3, 8, 9

SG501600R
пол — пом. 4, 5, 6, 7

610010001195
стены — пом. 6, 7

Tikkurila V503 Winter, LRV 86
Tikkurila Harmony, матовая
стены, потолок, плинтус — пом. 1, 9

NCS S 1502-Y50R, LRV 72
глубокоматовая
стены — пом. 2, 4, 5

NCS S 0300-N, LRV 92
глубокоматовая
потолок, плинтус — пом. 2, 3, 4, 5, 6, 7, 8

NCS S 1002-Y50R, LRV 82
стены — пом. 3

NCS S 0502-Y, LRV 86
матовая
стены — пом. 8

Farrow & Ball No. 241 Skimming Stone, LRV 67
Farrow & Ball Modern Emulsion, матовая
стены, плинтус — пом. 9

Текстиль и металл

Лён, Tikkurila H487
портьеры-волна

Вуаль, Tikkurila V503
тюль

Шерсть, Tikkurila V484
ковёр под кроватью

Букле, Farrow & Ball No. 229
подушки декоративные на кровать

Бархат, Farrow & Ball No. 47
подушки на кровать

Шерсть, Farrow & Ball No. 30
плед на кровать

Чёрный матовый металл
зеркало в рост

Чего избегаем

1) Холодный белый + серый ламинат + серый диван без дерева
2) Принты олени/hygge, надписи, лишние подушки
3) Глянцевый лак на дереве, венге, под орех
4) Одна люстра на комнату, свет 4000–6500 K, споты сеткой
5) Тяжёлые шторы с ламбрекенами, лепнина, многоуровневые потолки
6) Три разных светлых дуба в одном помещении

Допущения и предложения на листе

Основа листа: размеры сняты с растрового плана заказчика без размеров: масштаб восстановлен по площадям помещений (≈ 11,8 мм на пиксель), контрольный обмер не выполнен (К-1); высота потолка 2700 мм принята: на плане заказчика её нет (К-2); толщины стен 300 / 120 мм приняты по плану заказчика, не замерены (К-1); разрешённая мощность 15 кВт принята по типовым ТУ для квартиры, ТУ заказчиком не переданы (К-4).

См. лист открытых вопросов (лист 5, записи К-1, К-2, К-4).

Примечания

1. Коды цвета — по веерам производителей (колерная карта, лист 36); перед закупкой краски — выкрас на стене объекта под дневным светом и лампами проекта.
2. Материалы — по ведомости отделки (лист 35); мебель, текстиль и декор — по спецификации (лист 16). Образцы доски, керамогранита и тканей утвердить до заказа.
3. Фактуры на листе условные, цвет передан по HEX-значениям производителей: при печати возможны отклонения, решение — только по физическому образцу.

Изм.	Кол.уч	Лист	№ док.	Подп.	Дата
Разраб.		Кырпан А.С.			09.10.26
Пров.					
ГИП					
Н. контр.					
Утв.					

ГД-2026-007-АИ

Квартира 65 м²

Общая площадь 65,24* м² · * размеры со скана, не замерены (реестр — п. 5, К-1)

Дизайн-проект интерьера

Стадия	Лист	Листов
РП	14	79

Концепция интерьера


М 6/м

Кырпан Александр Сергеевич

выпуск 09.10.2026 № 147dabfd23 · стр. 18 из 110

План расстановки мебели

Мебель и оборудование · размеры в мм от чистовых стен · марки — по ведомости

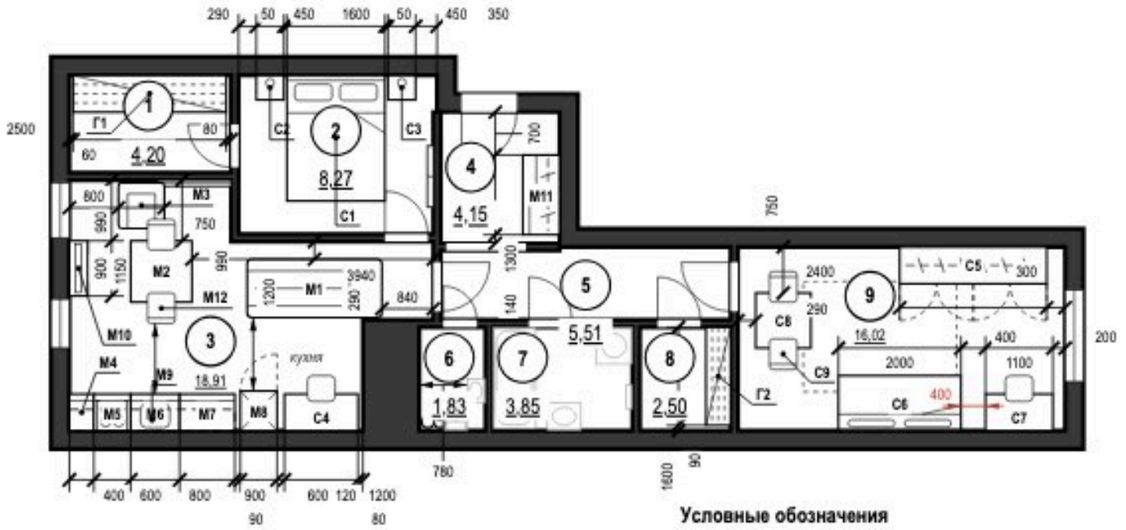

Условные обозначения

- мебель и оборудование — габарит в масштабе
- навесные шкафы (низ выше 0,9 м) — невидимый контур
- ковёр
- зона открывания дверец шкафов и техники
- K1 — марка предмета по ведомости мебели
- привязка от чистовой стены, мм
- ширина прохода, зазор, мм
- проход меньше нормы — расстановку изменить
- сантехприборы — подложка (лист ВК)
- радиатор отопления (лист ОВ)
- существующие стены (сечение)
- стояк: К1 — канализация, В1 — ХВС, Т3 — ГВС
- 1 — номер помещения, площадь м²
- зона — функциональная зона помещения

Экспликация помещений

лист 11 · на плане — номера в марках

Ведомость мебели и оборудования

Марка	Наименование	Ш×Г×В, мм	Пом.	Кол.
Г1	Система хранения	2500×600×2400	1	1
C1	Кровать двуспальная	1600×2050×450	2	1
C2	Тумба прикроватная	450×400×500	2	1
C3	Тумба прикроватная	450×400×500	2	1
M2	Стол обеденный круглый Ø1000	1000×1000×750	3	1
M3	Кресло	750×750×800	3	1
M10	ТВ на стене	900×300×450	3	1
M1	Диван	950×2200×850	3	1
C4	Стол рабочий	1200×600×750	3	1
M4	Модуль нижний	400×600×900	3	1
M5	Модуль нижний	600×600×900	3	1
M6	Модуль нижний	800×600×900	3	1
M7	Модуль нижний	900×600×900	3	1
M8	Пенал кухонный	600×650×2100	3	1
M9	Модуль навесной	2700×350×720	3	1
M11	Шкаф-купе	1300×600×2600	4	1
Г2	Стеллаж кладовой	1600×400×2400	8	1
C5	Шкаф распашной	2400×600×2400	9	1
C6	Кровать односпальная 900×2000	2000×900×450	9	1
C7	Стол письменный	1100×600×750	9	1
C8	Стол игровой круглый Ø900	900×900×600	9	1
M12	Стул обеденный к столу M2	450×500×820	3	2
C9	Стул обеденный к столу C8	450×500×820	9	2

Ш — вдоль стены (изголовья), Г — от стены (длина кровати)

Материалы, модели, допуск замены — лист 16

Примечания

1. Размеры даны в мм от чистовых поверхностей стен: слой штукатурки 20 мм по блоку и 5 мм шпаклёвки по ГКЛ учтён. Перед заказом встроенной мебели — контрольный обмер после штукатурки.
2. Привязки мебели — от стен и углов помещения, а не от другой мебели; ширина проходов и зазоров показана стрелками.
3. Розетки, выводы и выключатели под мебель — см. лист 18 «План розеток и электровыводов»; сантехприборы и выводы воды лист 27.
4. План расстановки не является документацией для изготовления мебели: изделия — по чертежам мебельщика; покупную мебель заменять только на изделия не больше габарита из спецификации (лист 16).
5. Встроенная мебель «стена в стену» — с зазором 10 мм с каждой стороны или с компенсаторами.
6. Отступ от стены, на плане не образмерен: М3 — 40 мм.
7. Стулья обеденной группы (М12 — 2 шт., С9 — 2 шт.) показаны в рабочем положении, задвинутыми под столешницу на 150 мм.

Допущения и предложения на листе

Основа листа: размеры сняты с растрового плана заказчика без размеров: масштаб восстановлен по площадям помещений (≈ 11,8 мм на пиксель), контрольный обмер не выполнен (К-1); высота потолка 2700 мм принята: на плане заказчика её нет (К-2); толщины стен 300 / 120 мм приняты по плану заказчика, не замерены (К-1); разрешённая мощность 15 кВт принята по типовым ТУ для квартиры, ТУ заказчиком не переданы (К-4).

Открытые вопросы и конфликты по листу: К-1, К-3.

См. лист открытых вопросов (лист 5, записи К-1–К-4).

1000 мм · печать 1:1

Изм.	Кол.уч	Лист	№ док.	Подп.	Дата
Разраб.		Кырпан А.С.			09.10.26
Пров.					
ГИП					
Н. контр.					
Утв.					

ГД-2026-007-АИ

Квартира 65 м²

Общая площадь 65,24* м² · * размеры со скана, не замерены (реестр — п. 5, К-1)

Дизайн-проект интерьера	Стадия	Лист	Листов
	РП	15	79

План расстановки мебели

М 1:100

Кырпан Александр Сергеевич

выпуск 09.10.2026 № 147dabfd23 · стр. 19 из 110

Спецификация мебели и оборудования

Форма 1 ГОСТ 21.110-2013 · позиции мебели — по плану расстановки

ПРЕДВАРИТЕЛЬНО · не для производства работ · открыто пунктов: 4 (реестр — л. 5)

Поз.	Наименование и техническая характеристика	Тип, марка, обозначение документа, опросного листа	Код продукции	Поставщик	Ед. измерения	Кол.	Масса 1 ед., кг	Примечание
	Мебель встроенная и корпусная (изготовление по чертежам мебельщика)							
Г1	Система хранения: штанги, полки, ящики; каркас и полки — ЛДСП, декор «дуб натуральный»; Ш×Г×В 2500×600×2400 мм			изготовление на заказ	шт.	1		пом. 1; крепление к стене
М4	Модуль нижний; корпус ЛДСП 16 мм, фасады МДФ эмаль; Ш×Г×В 400×600×900 мм			изготовление на заказ	шт.	1		пом. 3
М5	Модуль нижний, варочная; корпус ЛДСП 16 мм, фасады МДФ эмаль; Ш×Г×В 600×600×900 мм			изготовление на заказ	шт.	1		пом. 3
М6	Модуль нижний, мойка; корпус ЛДСП 16 мм, фасады МДФ эмаль; Ш×Г×В 800×600×900 мм			изготовление на заказ	шт.	1		пом. 3
М7	Модуль нижний; корпус ЛДСП 16 мм, фасады МДФ эмаль; Ш×Г×В 900×600×900 мм			изготовление на заказ	шт.	1		пом. 3
М8	Пенал кухонный, холодильник; корпус ЛДСП 16 мм, фасады МДФ эмаль; Ш×Г×В 600×650×2100 мм			изготовление на заказ	шт.	1		пом. 3
М9	Модуль навесной; корпус ЛДСП 16 мм, фасады МДФ эмаль; Ш×Г×В 2700×350×720 мм			изготовление на заказ	шт.	1		пом. 3
М11	Шкаф-купе; корпус ЛДСП, фасады — матовая эмаль в цвет стен (NCS S 1502-Y50R); Ш×Г×В 1300×600×2600 мм			изготовление на заказ	шт.	1		пом. 4
С5	Шкаф распашной; корпус ЛДСП, фасады — матовая эмаль в цвет стен (Farrow & Ball No. 241); Ш×Г×В 2400×600×2400 мм			изготовление на заказ	шт.	1		пом. 9
	Мебель покупная							
С1	Кровать двуспальная; мягкое изголовье, обивка — ткань, цвет NCS S 1500-N; Ш×Г×В 1600×2050×450 мм			аналог по характеристикам	шт.	1		пом. 2; замена ≤ габарита
С2, С3	Тумба прикроватная; шпон, дуб натуральный, матовое масло; Ш×Г×В 450×400×500 мм			аналог по характеристикам	шт.	2		пом. 2; замена ≤ габарита
М1	Диван; обивка — ткань, цвет NCS S 1500-N; Ш×Г×В 950×2200×850 мм			аналог по характеристикам	шт.	1		пом. 3; замена ≤ габарита
М2	Стол обеденный круглый Ø1000; шпон, дуб натуральный, матовое масло; Ш×Г×В 1000×1000×750 мм			аналог по характеристикам	шт.	1		пом. 3; замена ≤ габарита
М3	Кресло; обивка — ткань, цвет NCS S 1500-N; Ш×Г×В 750×750×800 мм			аналог по характеристикам	шт.	1		пом. 3; замена ≤ габарита
М10	ТВ на стене, тумба подвесная; шпон, дуб натуральный, матовое масло; Ш×Г×В 900×300×450 мм			аналог по характеристикам	шт.	1		пом. 3; замена ≤ габарита
М12	Стул обеденный к столу М2; обивка — ткань, цвет NCS S 1500-N; каркас — дуб натуральный; Ш×Г×В 450×500×820 мм			аналог по характеристикам	шт.	2		пом. 3; замена ≤ габарита
С4	Стол рабочий (кабинет); шпон, дуб натуральный, матовое масло; Ш×Г×В 1200×600×750 мм			аналог по характеристикам	шт.	1		пом. 3; замена ≤ габарита
Г2	Стеллаж кладовой; каркас и полки — ЛДСП, декор «дуб натуральный»; Ш×Г×В 1600×400×2400 мм			аналог по характеристикам	шт.	1		пом. 8; замена ≤ габарита
С6	Кровать односпальная 900×2000; мягкое изголовье, обивка — ткань, цвет NCS S 1500-N; Ш×Г×В 2000×900×450 мм			аналог по характеристикам	шт.	1		пом. 9; замена ≤ габарита

Примечания

1. Позиции мебели совпадают с марками на плане расстановки (лист 15); размеры Ш×Г×В — Ш вдоль стены, Г от стены.
2. Встроенная и корпусная мебель изготавливается по чертежам мебельщика после контрольного обмера; графы «Тип, марка» и «Код продукции» для неё не заполняются (ГОСТ 21.110-2013).
3. Покупные изделия — аналог по характеристикам: заменять только на изделия не больше указанного габарита и того же материала и цвета.
4. Материал и цвет, не указанные в данных изделия, приняты по концепции (лист 14): тон дерева — по полу, обивка — по вторичному цвету палитры; образцы согласовать до заказа.
5. Масса 1 ед. для изделий до 25 кг не указывается. Техника — по монтажным схемам изготовителя; выводы — по листам ЭОМ и ВК.

Допущения и предложения на листе

Основа листа: размеры сняты с растрового плана заказчика без размеров: масштаб восстановлен по площадям помещений (≈ 11,8 мм на пиксель), контрольный обмер не выполнен (К-1); высота потолка 2700 мм принята: на плане заказчика её нет (К-2); толщины стен 300 / 120 мм приняты по плану заказчика, не замерены (К-1); разрешённая мощность 15 кВт принята по типовым ТУ для квартиры, ТУ заказчиком не переданы (К-4).

См. лист открытых вопросов (лист 5, записи К-1, К-2, К-4).

Изм.	Кол.уч	Лист	№ док.	Подп.	Дата
Разраб.		Кырпан А.С.			09.10.26
Пров.					
ГИП					
Н. контр.					
Утв.					

ГД-2026-007-АИ

Квартира 65 м²

Общая площадь 65,24* м² · * размеры со скана, не замерены (реестр — п. 5, К-1)

Дизайн-проект интерьера	Стадия	Лист	Листов
	РП	16	79
Спецификация мебели и оборудования М 6/м	**Кырпан Александр Сергеевич**		

выпуск 09.10.2026 № 147dabfd23 · стр. 20 из 110

Спецификация мебели и оборудования (продолжение)

Форма 1 ГОСТ 21.110-2013 · позиции мебели — по плану расстановки

Поз.	Наименование и техническая характеристика	Тип, марка, обозначение документа, опросного листа	Код продукции	Поставщик	Ед. измерения	Кол.	Масса 1 ед., кг	Примечание
С7	Стол письменный; шпон, дуб натуральный, матовое масло; Ш×Г×В 1100×600×750 мм			аналог по характеристикам	шт.	1		пом. 9; замена ≤ габарита
С8	Стол игровой круглый Ø900; шпон, дуб натуральный, матовое масло; Ш×Г×В 900×900×600 мм			аналог по характеристикам	шт.	1		пом. 9; замена ≤ габарита
С9	Стул обеденный к столу С8; обивка — ткань, цвет NCS S 1500-N; каркас — дуб натуральный; Ш×Г×В 450×500×820 мм			аналог по характеристикам	шт.	2		пом. 9; замена ≤ габарита
	Техника встраиваемая и бытовая, светильники под розетки							
	Варочная панель встраиваемая, электрическая, в модуле М5			аналог по характеристикам	шт.	1		пом. 3; по схеме изготовителя
	Холодильник, в модуле М8			аналог по характеристикам	шт.	1		пом. 3; по схеме изготовителя
	Стиральная машина, место по листу ВК (П22); Ш×Г 600×600 мм			аналог по характеристикам	шт.	1		пом. 7; по схеме изготовителя
	Торшер, у поз. М3; абажур — ткань или опаловое стекло; лампа 3000 К			аналог по характеристикам	шт.	1		пом. 3; розетка — по плану розеток (ЭОМ)
	Текстиль							
Т7	Портьеры-волна; лён 100 %; цвет Tikkurila H487; карниз 1820 мм, высота 2610 мм, сборка 2			аналог по характеристикам	шт.	2		пом. 9
Т8	Тюль; полиэстер 100 %; цвет Tikkurila V503; карниз 1820 мм, высота 2610 мм, сборка 2,5			аналог по характеристикам	шт.	1		пом. 9
Т9	Ковёр под кроватью; шерсть 100 %; цвет Tikkurila V484; 2500×1800 мм			аналог по характеристикам	шт.	1		пом. 9; с подложкой
Т10	Подушки декоративные на кровать; букле (шерсть 60 %, полиэстер 40 %); цвет Farrow & Ball No. 229			аналог по характеристикам	шт.	3		пом. 9
Т11	Подушки на кровать, акцент; хлопковый бархат 100 %; цвет Farrow & Ball No. 47			аналог по характеристикам	шт.	2		пом. 9
Т12	Плед на кровать; шерсть мериноса 100 %; цвет Farrow & Ball No. 30			аналог по характеристикам	шт.	1		пом. 9
	Декор							
ДК3	Картина над кроватью: графика в паспарту, рама — дуб; 1000×700 мм; низ на 1300 мм от пола			аналог по характеристикам	шт.	1	4	пом. 9; крепление к стене
ДК4	Зеркало в рост в тонкой чёрной раме; рама — чёрный матовый; 600×1600 мм; низ на 300 мм от пола			аналог по характеристикам	шт.	1	12	пом. 9; крепление: анкер для пустотелых оснований, 4 шт.

Допущения и предложения на листе

Основа листа: размеры сняты с растрового плана заказчика без размеров: масштаб восстановлен по площадям помещений (≈ 11,8 мм на пиксель), контрольный обмер не выполнен (К-1); высота потолка 2700 мм принята: на плане заказчика её нет (К-2); толщины стен 300 / 120 мм приняты по плану заказчика, не замерены (К-1); разрешённая мощность 15 кВт принята по типовым ТУ для квартиры, ТУ заказчиком не переданы (К-4).

См. лист открытых вопросов (лист 5, записи К-1, К-2, К-4).

Изм.	Кол.уч	Лист	№ док.	Подп.	Дата
Разраб.		Кырпан А.С.			09.10.26
Пров.					
ГИП					
Н. контр.					
Утв.					

ГД-2026-007-АИ

Квартира 65 м²

Общая площадь 65,24* м² · * размеры со скана, не замерены (реестр — п. 5, К-1)

Дизайн-проект интерьера

Стадия	Лист	Листов
РП	17	79

Спецификация мебели и оборудования (продолжение)
М 6/м

Кырпан Александр Сергеевич

выпуск 09.10.2026 № 147dabfd23 · стр. 21 из 110

03

Электрооборудование


Кырлан Александр Сергеевич

выпуск 09.10.2026 № 147dabfd23 · стр. 22 из 110

План розеток и электровыводов

Розетки, выводы кабеля, щит · размеры в мм · высоты от чистого пола

ПРЕДВАРИТЕЛЬНО · не для производства работ · открыто пунктов: 4 (реестр — л. 5)

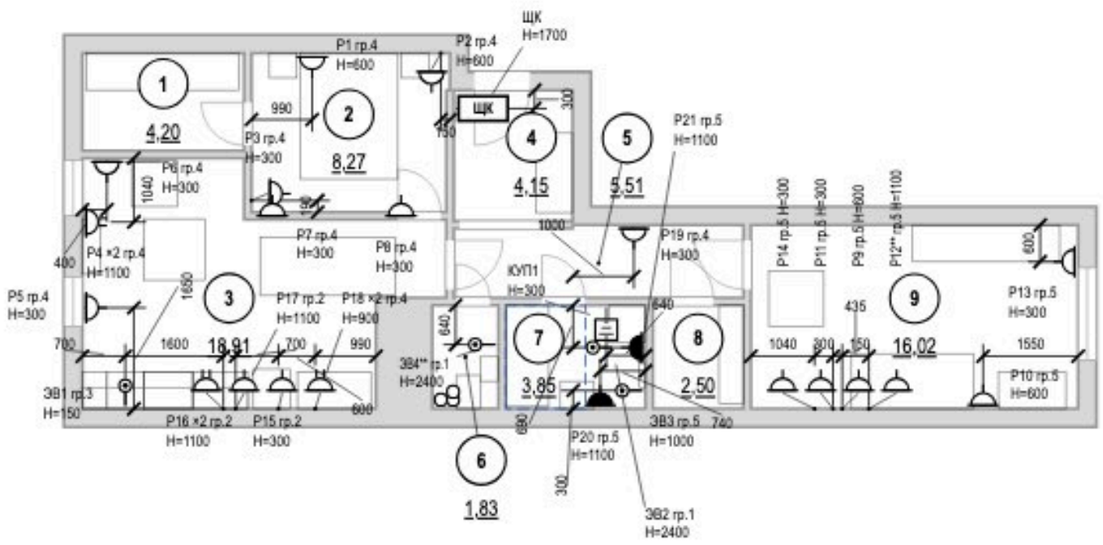

Условные обозначения

- розетка с заземляющим контактом; у знака — марка, ×N постов в рамке, гр. — группа щита, H — высота оси, мм
- то же, рамка на 2 поста (число черточек — число постов)
- розетка влагозащищённая IP44
- вывод кабеля для подключения прибора (без розетки), марка ЭВ
- КУП — коробка уравнивания потенциалов (ДСУП), проводник к шине PE щита
- ЩК — щит квартирный
- знак разведён для читаемости: точка на стене — у выноски, привязка — до неё
- граница зоны 2 ванной (600 мм от ванны/поддона)
- мебель и сантехприборы — подложка
- стояк К1 — канализация, В1 — ХВС, Т3 — ГВС
- 1 — номер помещения, площадь м²

Допущения и предложения на листе

Основа листа: размеры сняты с растрового плана заказчика без размеров: масштаб восстановлен по площадям помещений (≈ 11,8 мм на пиксель), контрольный обмер не выполнен (К-1); высота потолка 2700 мм принята: на плане заказчика её нет (К-2); толщины стен 300 / 120 мм приняты по плану заказчика, не замерены (К-1); разрешённая мощность 15 кВт принята по типовым ТУ для квартиры, ТУ заказчиком не переданы (К-4).

Знак «**» — предложение проектировщика, заказчиком не утверждено (согласовать с заказчиком): записи в реестре нет: P12 — высота 1100 мм выше нормы 1 м (ПУЭ 6.6.30) по назначению: питание ТВ над комодом, в одной зоне с выводами TB2 и LAN2; ЭВ4 — вывод к бытовому вентилятору, таймер выбега.

Открытые вопросы и конфликты по листу: К-4.

См. лист открытых вопросов (лист 5, записи К-1, К-2, К-4).

Примечания

1. За отметку 0,000 принят уровень чистого пола. Высоты H — от чистого пола до оси изделия; привязки — от чистовой грани стены до оси механизма (у рамки на несколько постов — до оси рамки).
2. Высота установки, не указанная на плане: розетки — 300 мм от чистого пола; выводы кабеля — по паспорту прибора.
3. Розетки в санузле — только вне зон 0–2 (ПУЭ 7.1.48, ГОСТ Р 50571.7.701-2024), IP44, через УЗО 30 мА.
4. Розеточные и мокрые линии — через УЗО или дифавтомат с током утечки не более 30 мА (ПУЭ 7.1.79); в санузле выполнить ДСУП (ПУЭ 7.1.87–7.1.88).
5. Кабель — медный, исполнение нг(A)-LS (ГОСТ 31565-2012); скрытая прокладка только горизонтально и вертикально, фактические трассы зафиксировать исполнительной схемой до закрытия отделкой.
6. Расчёт нагрузок, токов КЗ, селективности и сечений — по проекту ЭОМ организации с допуском СРО; лист задаёт состав, расположение и группы.
7. Выводы кухонной техники — после утверждения проекта кухни (ориентировочно); привязки выводов даны от осей модулей гарнитура и пересматриваются вместе с проектом кухни.
8. Ведомости электроточек, изделий, светильников и расшифровка клавиш — лист 21.

1000 мм · печать 1:1

Изм.	Кол.уч	Лист	№ док.	Подп.	Дата
Разраб.		Кырлан А.С.			09.10.26
Пров.					
ГИП					
Н. контр.					
Утв.					

ГД-2026-007-АИ

Квартира 65 м²

Общая площадь 65,24* м² · * размеры со скана, не замерены (реестр — л. 5, К-1)

Дизайн-проект интерьера

Стадия	Лист	Листов
РП	18	79

План розеток и электровыводов

М 1:100


Кырлан Александр Сергеевич

выпуск 09.10.2026 · 147dabfd23 · стр. 23 из 110

План освещения

Светильники, группы включения, извещатели · размеры в мм

ПРЕДВАРИТЕЛЬНО · не для производства работ · открыто пунктов: 4 (реестр — л. 5)

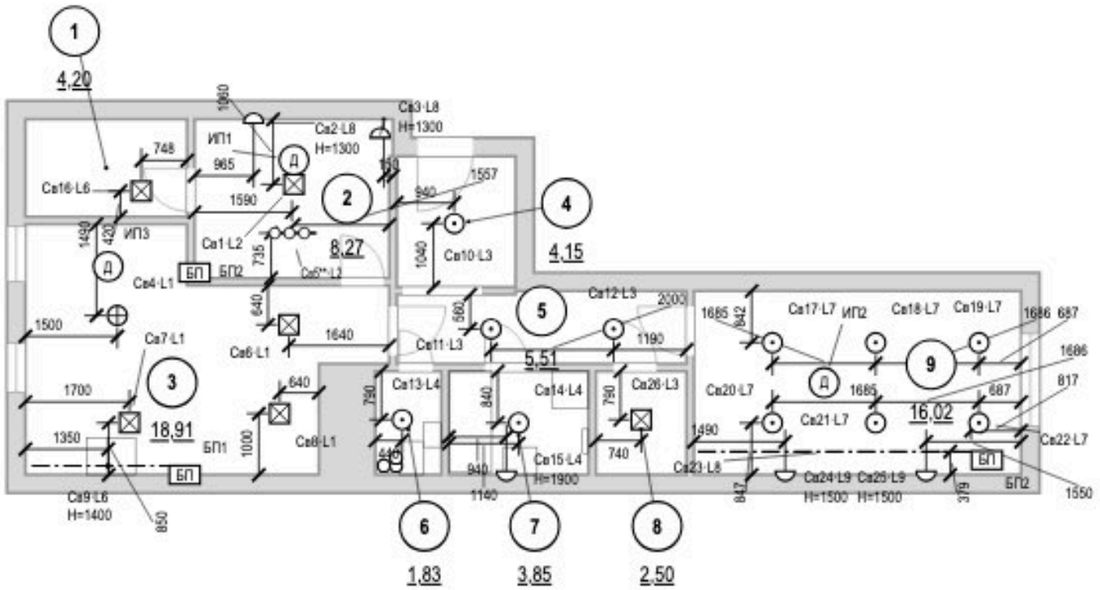

Условные обозначения

- светильник встраиваемый точечный
- светильник потолочный накладной
- светильник подвесной
- светильник настенный (бра), H — высота оси
- линейный светильник настенный (подсветка столешницы), точка — вывод питания
- светодиодная лента в профиле / в карнизе короба
- трековая система
- Св1·L1 — марка светильника (как в ведомости и на развёртках) · группа включения L (лист выключателей)
- Д — извещатель пожарный дымовой автономный
- БП — блок питания LED, с доступом (люк от 100×100 мм)
- 1 — номер помещения, площадь м²

Освещённость (оценка)

Пом.	S, м²	Ен, лк	Φ треб., лм	Φ по пр., лм
1	4,2	75	890	900
2	8,3	150	3490	5000
3	18,9	150	7990	6300
4	4,2	50	580	800
5	5,5	50	780	1600
6	1,8	50	260	500
7	3,9	50	540	700
8	2,5	30	210	600
9	16	200	9030	6300

Допущения и предложения на листе

Основа листа: размеры сняты с растрового плана заказчика без размеров: масштаб восстановлен по площадям помещений (≈ 11,8 мм на пиксель), контрольный обмер не выполнен (К-1); высота потолка 2700 мм принята: на плане заказчика её нет (К-2); толщины стен 300 / 120 мм приняты по плану заказчика, не замерены (К-1); разрешённая мощность 15 кВт принята по типовым ТУ для квартиры, ТУ заказчиком не переданы (К-4).

Знак «**» — предложение проектировщика, заказчиком не утверждено (согласовать с заказчиком): записи в реестре нет: Св6 — трековая система 2 × 900 лм: светильник добавлен проектировщиком, поток принят до нормы освещённости, модель и паспорт не выбраны.

См. лист открытых вопросов (лист 5, записи К-1, К-2, К-4).

Примечания

1. За отметку 0,000 принят уровень чистого пола. Высоты H — от чистого пола до оси изделия; привязки — от чистовой грани стены до оси механизма (у рамки на несколько постов — до оси рамки).
2. Высота установки, не указанная на плане: светильники — на потолке; настенные — по отметке H у знака. Привязки — до оси светильника от чистовой грани стены, по рядам.
3. Освещённость: Ен — СанПиН 1.2.3685-21, табл. 5.52 (на полу); Φ треб. = Ен·Sr(U·MF) при U = 0,5 и MF = 0,71 (СП 52.13330.2016, табл. 4.3) — оценка, не светотехнический расчёт. Декоративная подсветка в Φ не входит.
4. Во влажных помещениях — светильники не ниже IP44; в зонах 0–2 ванной — по ГОСТ Р 50571.7.701-2024 (зона 1 — IPX5).
5. Розеточные и мокрые линии — через УЗО или дифавтомат с током утечки не более 30 мА (ПУЭ 7.1.79); в санузле выполнить ДСУП (ПУЭ 7.1.87–7.1.88).
6. Кабель — медный, исполнение нг(A)-LS (ГОСТ 31565-2012); скрытая прокладка только горизонтально и вертикально, фактические трассы зафиксировать исполнительной схемой до закрытия отделкой.
7. Расчёт нагрузок, токов КЗ, селективности и сечений — по проекту ЭОМ организации с допуском СРО; лист задаёт состав, расположение и группы.
8. Ведомость светильников — лист 21.

1000 мм · печать 1:1

Изм.	Кол.уч	Лист	№ док.	Подп.	Дата
Разраб.		Кырпан А.С.			09.10.26
Пров.					
ГИП					
Н. контр.					
Утв.					

ГД-2026-007-АИ

Квартира 65 м²

Общая площадь 65,24* м² · * размеры со скана, не замерены (реестр — л. 5, К-1)

Дизайн-проект интерьера

Стадия	Лист	Листов
РП	19	79

План освещения


М 1:100

Кырпан Александр Сергеевич

выпуск 09.10.2026 № 147dabfd23 · стр. 24 из 110

План выключателей и схема включения

Выключатели S, группы включения L, линии связи · размеры в мм

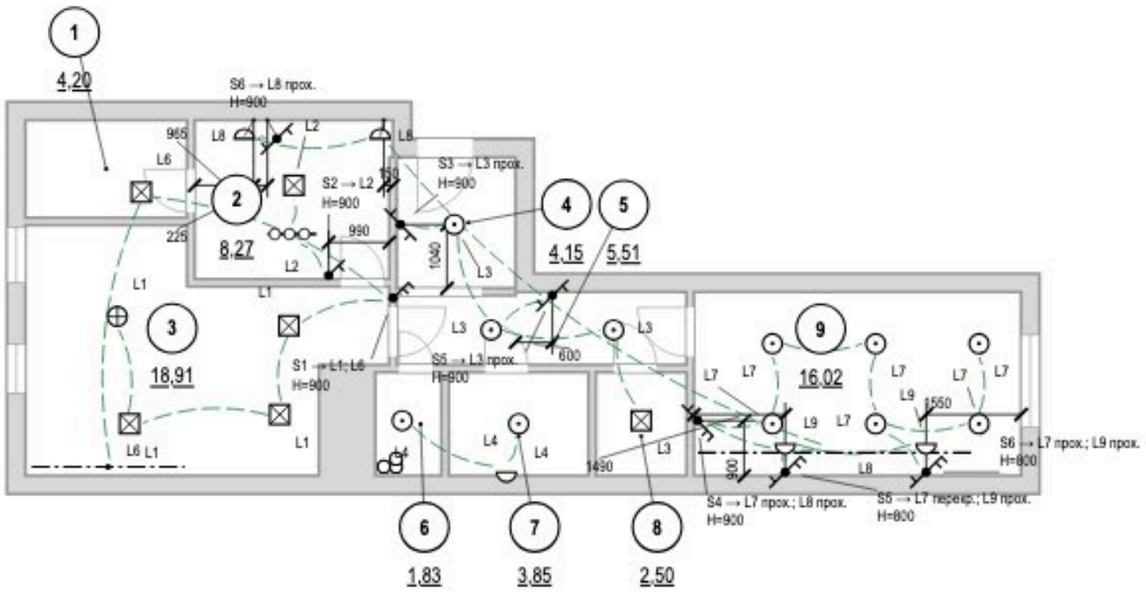

Условные обозначения

- выключатель одноклавишный
- выключатель двухклавишный (флажков — по числу клавиш)
- выключатель с проходной или перекрёстной клавишей (обратный флажок); тип клавиши — в подписи
- S1 → — марка → группы по клавишам (через «;»): прох. — проходной, перекр. — перекрёстный, дим. — светорегулятор; H — высота
- линия связи: выключатель → светильники группы (не трасса кабеля)
- светильник встраиваемый точечный
- светильник потолочный накладной
- светильник подвесной
- светильник настенный (бра), H — высота оси
- линейный светильник настенный (подсветка столешницы), точка — вывод питания
- светодиодная лента в профиле / в карнизе короба
- трековая система
- L1 — группа включения у светильника
- (1) — номер помещения, площадь м²

Допущения и предложения на листе

Основа листа: размеры сняты с растрового плана заказчика без размеров: масштаб восстановлен по площадям помещений (≈ 11,8 мм на пиксель), контрольный обмер не выполнен (К-1); высота потолка 2700 мм принята: на плане заказчика её нет (К-2); толщины стен 300 / 120 мм приняты по плану заказчика, не замерены (К-1); разрешённая мощность 15 кВт принята по типовым ТУ для квартиры, ТУ заказчиком не переданы (К-4).

См. лист открытых вопросов (лист 5, записи К-1, К-2, К-4).

Примечания

1. За отметку 0,000 принят уровень чистого пола. Высоты H — от чистого пола до оси изделия; привязки — от чистовой грани стены до оси механизма (у рамки на несколько постов — до оси рамки).
2. Высота установки, не указанная на плане: выключатели — 900 мм от чистого пола, со стороны дверной ручки (ПУЭ 7.1.51).
3. Линии связи показывают, какой выключатель какую группу L включает; это не трасса кабеля. Трасса — принципиальная, фактическую зафиксировать исполнительной схемой.
4. Группы из нескольких мест (L8 — S4, S6; L3 — S3, S5; L7 — S4, S5, S6; L9 — S5, S6): на крайних местах — проходные клавиши, на промежуточных — перекрёстные; механизмы — в ведомости изделий.
5. Вентиляторы санузлов (выводы ЭВ на плане розеток) включаются вместе с основным светом помещения, отключаются с задержкой — таймер выбега в вентиляторе.
6. Розеточные и мокрые линии — через УЗО или дифавтомат с током утечки не более 30 мА (ПУЭ 7.1.79); в санузле выполнить ДСУП (ПУЭ 7.1.87–7.1.88).
7. Кабель — медный, исполнение нг(A)-LS (ГОСТ 31565-2012); скрытая прокладка только горизонтально и вертикально, фактические трассы зафиксировать исполнительной схемой до закрытия отделкой.
8. Расчёт нагрузок, токов КЗ, селективности и сечений — по проекту ЭОМ организации с допуском СРО; лист задаёт состав, расположение и группы.
9. Группы без выключателя: L4 — назначить управление до монтажа.
10. Расшифровка клавиш и ведомость изделий — лист 21.

1000 мм · печать 1:1

Изм.	Кол.уч	Лист	№ док.	Подп.	Дата
Разраб.		Кырпан А.С.			09.10.26
Пров.					
ГИП					
Н. контр.					
Утв.					

ГД-2026-007-АИ

Квартира 65 м²

Общая площадь 65,24* м² · * размеры со скана, не замерены (реестр — п. 5, К-1)

Дизайн-проект интерьера

Стадия	Лист	Листов
РП	20	79

План выключателей и схема включения

М 1:100

Кырпан Александр Сергеевич

выпуск 09.10.2026 № 147dabfd23 · стр. 25 из 110

Ведомость электроточек и изделий

Электроточки, изделия, светильники, клавиши выключателей · б/м

Ведомость электроточек

Марка	Пом.	Назначение	Н, мм	Гр.
Р1	2	розетка общего назначения	600	4
Р2	2	розетка общего назначения	600	4
Р3	2	комод, зарядка	300	4
Р4	3	ТВ, приставка	1100	4
Р5	3	обеденная зона	300	4
Р6	3	торшер у кресла	300	4
Р7	3	у дивана	300	4
Р8	3	у дивана	300	4
Р15	3	холодильник	300	2
Р16	3	рабочая зона	1100	2
Р17	3	рабочая зона	1100	2
Р18	3	рабочее место	900	4
ЭВ1	3	варочная панель	150	3
ЩК	4	щит квартирный	1700	
Р19	5	уборка	300	4
ЭВ4*	6	вентилятор ВР2 (таймер выбега)	2400	1
ЮУП1	7	ЮУП	300	
Р20	7	фен, IP44	1100	5
Р21	7	стиральная машина, IP44	1100	5
ЭВ2	7	вентилятор (клавиша L4, таймер выбега)	2400	1
ЭВ3	7	полотенцесушитель, IP44	1000	5
Р9	9	у кровати	600	5
Р10	9	у кровати	600	5
Р11	9	у комода	300	5
Р12*	9	ТВ над комодом (в одной зоне с ТВ2, LAN2)	1100	5
Р13	9	уборка	300	5
Р14	9	уборка у входа	300	5

Ведомость изделий

Наименование	Марки	Ед.	Кол.
Розетка с з/к и защитными шторками, 16 А	по ведомости точек	шт	22
Розетка IP44 с крышкой, 16 А	Р20, Р21	шт	2
Выключатель 1-клав.	S2	шт	1
Выключатель 1-клав. проходной	S3, S5, S6	шт	3
Выключатель 2-клав.	S1	шт	1
Выключатель 2-клав. (перекрёстная + проходная)	S5	шт	1
Выключатель 2-клав. проходной	S4, S6	шт	2
Рамка 1-постовая	в т. ч. 8 под выключ.	шт	26
Рамка 2-постовая		шт	3
Коробка установочная (подрозетник) Ø68	розетки, выключатели	шт	32
Вывод кабеля под прибор (клеммник)	ЭВ1–ЭВ3	шт	3
Вывод кабеля к вентилятору вытяжки	ЭВ4*	шт	1
Коробка уравнивания потенциалов КУП	ЮУП1	шт	1
Блок питания LED 24 В, 60 Вт	БП1, БП2	шт	2
Блок питания LED 24 В, 200 Вт, дим.	БП2	шт	1
Извещатель дымовой автономный	ИП1–ИП3	шт	3
Щит квартирный (состав — лист щита)	ЩК	шт	1
Розетка компьютерная RJ45, кат. 6, с рамкой и подрозетником	LAN1, LAN2	шт	4
Розетка телевизионная (коаксиальная) с рамкой и подрозетником	ТВ1, ТВ2	шт	2
Трубка или монитор домофона (поставка домофонной организации)	ДФ1	шт	1
Щит слаботочный ЩС**: корпус, DIN-рейка, розетки 220 В	ЩС*	шт	1
Патч-панель, портов не менее 4		шт	1
Коммутатор, портов не менее 4, из них PoE 0		шт	1
Кабель домофона — тип по системе поставщика (по лучам от ЩС**, запас 10 %)		м	3,1

Ведомость изделий (продолжение)

Наименование	Марки	Ед.	Кол.
Кабель коаксиальный RG-6 (75 Ом) к розеткам ТВ (по лучам от ЩС**, запас 10 %)		м	30,2
Кабель U/UTP кат. 5е (LAN, Wi-Fi и камеры по PoE) (по лучам от ЩС**, запас 10 %)		м	42,7
Кабель U/UTP кат. 6 (LAN, Wi-Fi и камеры по PoE) (по лучам от ЩС**, запас 10 %)		м	14,2

Ведомость светильников

Поз.	Марки	Тип	Кол.	P, Вт	Ф, лм	IP	Tц/Ra
1	Св16	потолочный накладной	1	10	900		300090
2	Св1	потолочный накладной	1	36	3200		270090
3	Св5*	трековая система	2	12	900		270090
4	Св2, Св3	настенный (бра), H=1300	2	4	250		270090
5	Св4	подвесной	1	24	2400		300090
6	Св6	потолочный накладной	1	18	1800		300090
7	Св7	потолочный накладной	1	12	1100		300090
8	Св8	потолочный накладной	1	12	1000		400090
9	Св9	линейный светильник, H=1400	1	18	1300		300090
10	Св10–Св12	встраиваемый точечный	3	9	800		300090
11	Св13	встраиваемый точечный	1	6	500		300090
12	Св14	встраиваемый точечный	1	9	700	44	300090
13	Св15	настенный (бра), H=1900	1	6	400	44	300090
14	Св26	потолочный накладной	1	9	600		300090
15	Св17–Св22	встраиваемый точечный	6	12	1050		270090
16	Св23	светодиодная лента, 12,3 м	1	118,1	11070		270090
17	Св24, Св25	настенный (бра), H=1500	2	6	400		270090

Расшифровка клавиш

Марка	Пом.	Н, мм	Клав.	Механизм	Группа: светильники
S1	3	900	1	обычный	L1: Св4, Св6–Св8
			2	обычный	L6: Св9, Св16
S2	2	900	1	обычный	L2: Св1, Св5*
S3	4	900	1	проходной	L3: Св10–Св12, Св26
S4	9	900	1	проходной	L7: Св17–Св22
			2	проходной	L8: Св2, Св3, Св23
S5	5	900	1	проходной	L3: Св10–Св12, Св26
S5	9	800	1	перекрёстный	L7: Св17–Св22
			2	проходной	L9: Св24, Св25
S6	2	900	1	проходной	L8: Св2, Св3, Св23
S6	9	800	1	проходной	L7: Св17–Св22
			2	проходной	L9: Св24, Св25

Допущения и предложения на листе

Основа листа: размеры сняты с растрового плана заказчика без размеров: масштаб восстановлен по площадям помещений (≈ 11,8 мм на пиксель), контрольный обмер не выполнен (К-1); высота потолка 2700 мм принята: на плане заказчика её нет (К-2); толщины стен 300 / 120 мм приняты по плану заказчика, не замерены (К-1); разрешённая мощность 15 кВт принята по типовым ТУ для квартиры, ТУ заказчиком не переданы (К-4).

Знак «*» — предложение проектировщика, заказчиком не утверждено (согласовать с заказчиком): записи в реестре нет: Св5 — трековая система 2 × 900 лм: светильник добавлен проектировщиком, поток принят до нормы освещённости, модель и паспорт не выбраны; Р12 — высота 1100 мм выше нормы 1 м (ПУЭ 6.6.30) по назначению: питание ТВ над комодом, в одной зоне с выводами ТВ2 и LAN2; ЭВ4 — вывод к бытовому вентилятору, таймер выбега; ЩС — щит слаботочный: место и состав.

См. лист открытых вопросов (лист 5, записи К-1, К-2, К-4).

Примечания

1. Ведомости сведены с планов розеток, освещения и выключателей; марки, группы и высоты — те же, что у знаков на планах.
2. Механизмы, рамки и светорегуляторы — одной серии; число постов и клавиш сверено с выбранной серией. Перекрёстная клавиша — отдельный механизм серии.
3. За отметку 0,000 принят уровень чистого пола. Высоты H — от чистого пола до оси изделия; привязки — от чистовой грани стены до оси механизма (у рамки на несколько постов — до оси рамки).
4. Розеточные и мокрые линии — через УЗО или дифавтомат с током утечки не более 30 мА (ПУЭ 7.1.79); в санузле выполнить ДСУП (ПУЭ 7.1.87–7.1.88).
5. Кабель — медный, исполнение нг(A)-LS (ГОСТ 31565-2012); скрытая прокладка только горизонтально и вертикально, фактические трассы зафиксировать исполнительной схемой до закрытия отделкой.
6. Расчёт нагрузок, токов КЗ, селективности и сечений — по проекту ЭОМ организации с допуском СРО; лист задаёт состав, расположение и группы.

Изм.	Кол.уч	Лист	№ док.	Подп.	Дата
Разраб.		Кырпан А.С.			09.10.26
Пров.					
ГИП					
Н. контр.					
Утв.					

ГД-2026-007-АИ

Квартира 65 м²

Общая площадь 65,24* м² · * размеры со скана, не замерены (реестр — л. 5, К-1)

Дизайн-проект интерьера

Стадия	Лист	Листов
РП	21	79

Ведомость электроточек и изделий


М б/м

Кырпан Александр Сергеевич

выпуск 09.10.2026 · 147dabfd23 · стр. 26 из 110

Однолинейная схема щита

Щит квартирный ЩК · без масштаба

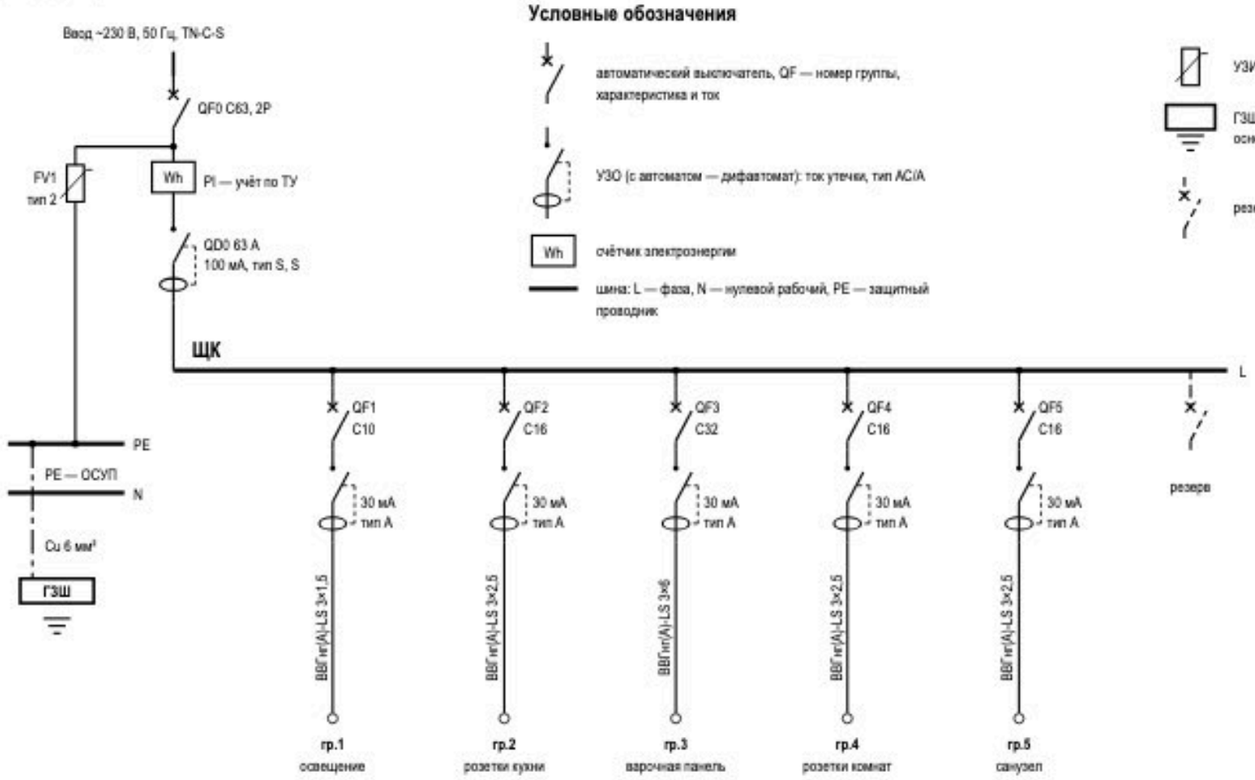

Условные обозначения

- автоматический выключатель, QF — номер группы, характеристика и ток
- УЗО (с автоматом — дифавтомат): ток утечки, тип AC/A
- Wh — счётчик электроэнергии
- шина: L — фаза, N — нулевой рабочий, PE — защитный проводник
- УЗИП (ограничитель перенапряжений), FV — марка
- ГЗШ — главная заземляющая шина; штрихпунктир — проводник основной системы уравнивания потенциалов (ОСУП)
- резервный аппарат (не менее 20 % групп)

Данные щитка

Показатель	Значение
Номер щитка	ЩК
Тип	ЩРВ-П-24, IP41
Уст. мощность, кВт	
Разреш. мощность, кВт	15
Расчётная, кВт	9,8
Автоматы 1гс занят. / рез.	5 / 1
Модулей: всего / занято	24 / 16
Ток на вводе, А	63
Вводной аппарат	QF0 C63, 2P
УЗИП	FV1, тип 2, ЩК, после счётчика
ГЗШ, проводник ОСУП	Cu 6 мм²

Таблица групп щита ЩК и кабельный журнал

№	Назначение	Помещения	Автомат	УЗО / дифавтомат	Кабель	Длина, м	Р, кВт	Точек
1	освещение	1, 2, 3, 4, 5, 6, 7, 8, 9	C10	30 мА, тип A	ВВГнг(A)-LS 3×1,5	138,2		38
2	розетки кухни	3	C16	30 мА, тип A	ВВГнг(A)-LS 3×2,5	19,3		3
3	варочная панель	3	C32	30 мА, тип A	ВВГнг(A)-LS 3×6	17,3		1
4	розетки комнат	2, 3, 5	C16	30 мА, тип A	ВВГнг(A)-LS 3×2,5	52,4		10
5	санузел	7, 9	C16	30 мА, тип A	ВВГнг(A)-LS 3×2,5	43,8		9
	Итого по сечениям ВВГнг(A)-LS, м: 3×1,5 — 138,2; 3×2,5 — 115,5; 3×6 — 17,3					271		

Примечания

1. Схема однолинейная: одна линия — фаза, N и PE группы; аппараты — в отключённом положении (ГОСТ 2.702, ГОСТ 2.755). Номера групп — как у точек на планах (гр.). За отметку 0,000 принят уровень чистого пола; высота щита — по плану розеток.
2. Розеточные и мокрые линии — через УЗО или дифавтомат с током утечки не более 30 мА (ПУЭ 7.1.79); в санузле выполнить ДСУП (ПУЭ 7.1.87–7.1.88).
3. УЗО тип A — для линий с электроникой, стиральной и посудомоечной машиной, LED-драйверами; тип AC — только для чисто активной нагрузки.
4. Кабель — медный, исполнение нг(A)-LS (ГОСТ 31565-2012); скрытая прокладка только горизонтально и вертикально, фактические трассы зафиксировать исполнительной схемой до закрытия отделкой.
5. Номинал автомата — не выше допустимого тока кабеля: 1,5 мм² — до 10 А, 2,5 мм² — до 16 А. Резерв щита — не менее 20 % модулей.
6. Расчёт нагрузок, токов КЗ, селективности и сечений — по проекту ЭОМ организации с допуском СРО; лист задаёт состав, расположение и группы.
7. УЗИП FV1 — после вводного автомата, проводник к шине PE — кратчайший, без петель. Шина PE щита соединяется с ГЗШ проводником ОСУП; к ГЗШ присоединяются трубы водопровода и отопления на вводе в квартиру (ПУЭ 7.1.67). Шины N и PE — раздельные, после разделения PEN не объединяются.
8. До подключения нагрузки — приёмо-сдаточные испытания с протоколом: сопротивление изоляции линий не менее 0,5 МОм, срабатывание УЗО по току и времени, непрерывность защитных проводников PE (ПУЭ, гл. 1.8).

Допущения и предложения на листе

Основа листа: размеры сняты с растрового плана заказчика без размеров: масштаб восстановлен по площадям помещений (≈ 11,8 мм на пиксель), контрольный обмер не выполнен (К-1); высота потолка 2700 мм принята: на плане заказчика её нет (К-2); толщины стен 300 / 120 мм приняты по плану заказчика, не замерены (К-1); разрешённая мощность 15 кВт принята по типовым ТУ для квартиры, ТУ заказчиком не переданы (К-4).

Открытые вопросы и конфликты по листу: К-4.

См. лист открытых вопросов (лист 5, записи К-1, К-2, К-4).

Изм.	Кол.уч	Лист	№ док.	Подп.	Дата
Разраб.		Кырпан А.С.			09.10.26
Пров.					
ГИП					
Н. контр.					
Утв.					

ГД-2026-007-АИ

Квартира 65 м²

Общая площадь 65,24* м² · * размеры со скана, не замерены (реестр — п. 5, К-1)

Дизайн-проект интерьера

Стадия	Лист	Листов
РП	22	79

Однолинейная схема щита

М 6/м


Кырпан Александр Сергеевич

выпуск 09.10.2026 · 147dabfd23 · стр. 27 из 110

План принципиальных трасс

Силовые трассы и объёмы электромонтажа, слаботочка в объёмах · размеры в мм

ПРЕДВАРИТЕЛЬНО · не для производства работ · открыто пунктов: 4 (реестр — л. 5)

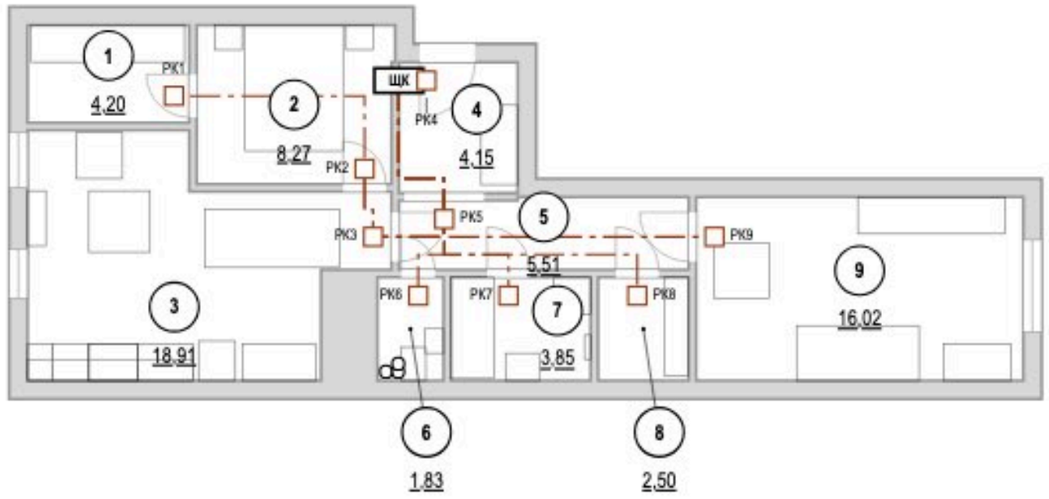

Кабель по группам ВВГнг(А)-LS, м

Гр.	мм²	Трасса	Данные
1	3×1,5	138,2	
2	3×2,5	19,3	
3	3×6	17,3	
4	3×2,5	52,4	
5	3×2,5	43,8	
Σ		**271**	

Экспликация помещений

№	Помещение	Площадь, м²
1	Гардеробная	4,20
2	Спальня	8,27
3	Кухня-гостиная	18,91
4	Прихожая	4,15
5	Коридор	5,51
6	Санузел	1,83
7	Ванная	3,85
8	Кладовая	2,50
9	Детская	16,02
	Итого (общая площадь)	65,24

Объёмы прокладки

Работа, материал	Ед.	Кол.
Гофротруба Ø20 в потолочном пространстве	м	97,8
Кабель-канал плинтуса для силовых линий	м	77,3
Короб или накладной канал для вертикальных спусков и подъёмов	м	50,6
Коробка распределительная (РК) над дверью помещения	шт	9
Слаботочка: кабель домофона	м	3,1
Слаботочка: Кабель коаксиальный RG-6 (75 Ом) к розеткам ТВ	м	30,2
Слаботочка: Кабель U/UTP кат. 5e (LAN, Wi-Fi и камеры по PoE)	м	42,7
Слаботочка: U/UTP кат. 6 (LAN, Wi-Fi, камеры)	м	14,2
Слаботочка: гофротруба Ø20 отдельно от силовых	м	81,2

Штробы — только после заключения

Работа	Ед.	Кол.
Вертикальные штробы 20×20 мм от потолка до каждой настенной точки (в маршрут без штроб не входят)	м	68,21

Условные обозначения

- ЩК — щит квартирный
- РК — распределительная коробка над дверью помещения
- магистраль от щита к РК: потолочное пространство, гофра
- мебель и сантехприборы — подложка

Допущения и предложения на листе

Основа листа: размеры сняты с растрового плана заказчика без размеров: масштаб восстановлен по площадям помещений (≈ 11,8 мм на гипсель), контрольный обмер не выполнен (К-1); высота потолка 2700 мм принята: на плане заказчика её нет (К-2); толщины стен 300 / 120 мм приняты по плану заказчика, не замерены (К-1); разрешённая мощность 15 кВт принята по типовым ТУ для квартиры, ТУ заказчиком не переданы (К-4).

Знак «**» — предложение проектировщика, заказчиком не утверждено (согласовать с заказчиком): записи в реестре нет: ЩС — щит слаботочный: место и состав.

См. лист открытых вопросов (лист 5, записи К-1, К-2, К-4).

Примечания

1. За отметку 0,000 принят уровень чистого пола. Высоты Н — от чистого пола до оси изделия; привязки — от чистовой грани стены до оси механизма (у рамки на несколько постов — до оси рамки).
2. Розеточные и мокрые линии — через УЗО или дифавтомат с током утечки не более 30 мА (ПУЭ 7.1.79); в санузле выполнить ДСУП (ПУЭ 7.1.87–7.1.88).
3. Кабель — медный, исполнение нг(А)-LS (ГОСТ 31565-2012); скрытая прокладка только горизонтально и вертикально; фактические трассы зафиксировать исполнительной схемой до закрытия отделкой.
4. Расчёт нагрузок, токов КЗ, селективности и сечений — по проекту ЭОМ организации с допуском СРО; лист задаёт состав, расположение и группы.
5. Длины — по плану: от щита вверх в потолочное пространство, по дверям и коридору без захода в мокрые помещения к распределительной коробке над дверью, далее к точкам; вертикали считаются вниз и обратно (у последней точки цепочки — в один конец); запас 10 %. Трассы принципиальные: фактическую зафиксировать исполнительной схемой до закрытия отделкой.
6. Несущие стены не определены: штробы в стенах не выполнять. Маршрут проложен без штроб: горизонтали — за потолком в гофре (97,8 м) и в кабель-канале плинтуса (77,3 м), вертикали — в коробе или накладном канале (89,1 м кабеля). Точек: за потолком — 21, спуск из потолка — 8, по плинтусу — 11, плинтус и подъём — 22.
7. Вариант со штробами — работа после технического заключения: 68,21 м вертикальных штроб от потолка до каждой настенной точки; условие — только после технического заключения: стена не несущая (или вертикальная штроба в несущей согласована конструктором), глубина и ширина 20–25 мм, не в зонах 0–2 ванной. Без заключения и согласования конструктора в смету и в график эта работа не входит.
8. Слаботочные сети: кабели и точки считаются по лучам от ЩС** (лист слаботочных сетей): 90 м, портов патч-панели и коммутатора не менее 4. Изделия — в ведомости изделий.

1000 мм · печать 1:1

Изм.	Кол.уч	Лист	№ док.	Подп.	Дата
Разраб.		Кырпан А.С.			09.10.26
Пров.					
ГИП					
Н. контр.					
Утв.					

ГД-2026-007-АИ

Квартира 65 м²

Общая площадь 65,24* м² · * размеры со скана, не замерены (реестр — п. 5, К-1)

Дизайн-проект интерьера

Стадия	Лист	Листов
РП	23	79

План принципиальных трасс

М 1:100


Кырпан Александр Сергеевич

выпуск 09.10.2026 № 147dabfd23 · стр. 28 из 110

План слаботочных сетей

Интернет, ТВ, домофон · размеры в мм · высоты от чистого пола

ПРЕДВАРИТЕЛЬНО · не для производства работ · открыто пунктов: 4 (реестр — л. 5)

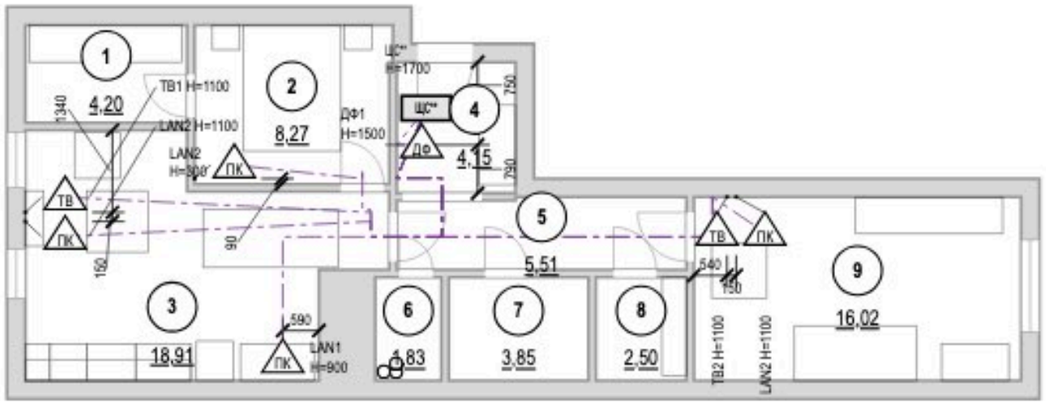

Ведомость слаботочных точек

Марка	Пом.	Назначение	H, мм	Кабель
LAN2	2	розетка LAN (RJ45)	300	U/UTP кат. 5e/6
TB1	3	розетка ТВ	1100	RG-6 (75 Ом)
LAN2	3	розетка LAN (RJ45)	1100	U/UTP кат. 5e/6
LAN1	3	розетка LAN (RJ45)	900	U/UTP кат. 5e/6
ДФ1	4	домофон (трубка)	1500	по системе
TB2	9	розетка ТВ	1100	RG-6
LAN2	9	розетка LAN (RJ45)	1100	U/UTP кат. 6
ЩС**	4	щит слаботочный	1700	ввод пров.

Условные обозначения

- ЩС — щит слаботочный: ввод провайдера, роутер, коммутатор
- ПК — розетка компьютерная RJ45
- ТВ — розетка телевизионная
- ДФ — трубка или монитор домофона
- кабель от ЩС до точки, отдельным лучом
- мебель и сантехприборы — подложка
- (1) — номер помещения, площадь м²

Допущения и предложения на листе

Основа листа: размеры сняты с растрового плана заказчика без размеров: масштаб восстановлен по площадям помещений (≈ 11,8 мм на пиксель), контрольный обмер не выполнен (К-1); высота потолка 2700 мм принята: на плане заказчика её нет (К-2); толщины стен 300 / 120 мм приняты по плану заказчика, не замерены (К-1); разрешённая мощность 15 кВт принята по типовым ТУ для квартиры, ТУ заказчиком не переданы (К-4).

Знак «**» — предложение проектировщика, заказчиком не утверждено (согласовать с заказчиком): записи в реестре нет: ЩС — щит слаботочный: место и состав.

См. лист открытых вопросов (лист 5, записи К-1, К-2, К-4).

Примечания

1. За отметку 0,000 принят уровень чистого пола. Высоты H — от чистого пола до оси изделия; привязки — от чистовой грани стены до оси механизма (у рамки на несколько постов — до оси рамки).
2. Высота установки, не указанная на плане: розетки LAN и ТВ — 300 мм от чистого пола.
3. Слаботочные кабели — отдельно от силовых: в своей трубе или лотке, при параллельной прокладке не ближе 100 мм к силовым, пересечения под прямым углом; каждую точку — отдельным кабелем от ЩС** без скруток.
4. Трассы на листе — принципиальные; фактические зафиксировать исполнительной схемой до закрытия отделкой. Силовые линии, УЗО 30 мА, ДСУП, кабель нг(A)-LS — по листам розеток и щита.
5. Проект силовой части и расчёт токов КЗ — по проекту ЭОМ; слаботочная часть согласуется с провайдером и управляющей компанией (домофон, коллективное ТВ).

1000 мм · печать 1:1

Изм.	Кол.уч	Лист	№ док.	Подп.	Дата
Разраб.		Кырпан А.С.			09.10.26
Пров.					
ГИП					
Н. контр.					
Утв.					

ГД-2026-007-АИ

Квартира 65 м²

Общая площадь 65,24* м² · * размеры со скана, не замерены (реестр — п. 5, К-1)

Дизайн-проект интерьера	Стадия	Лист	Листов
	РП	24	79

План слаботочных сетей

М 1:100

Кырпан Александр Сергеевич

выпуск 09.10.2026 № 147dabfd23 · стр. 29 из 110

04


Отопление и вентиляция

Кырлан Александр Сергеевич

выпуск 09.10.2026 № 147dabfd23 · стр. 30 из 110

План вентиляции

Вытяжка, приток, переток · кондиционирование не предусмотрено · размеры в мм · высоты от чистого пола

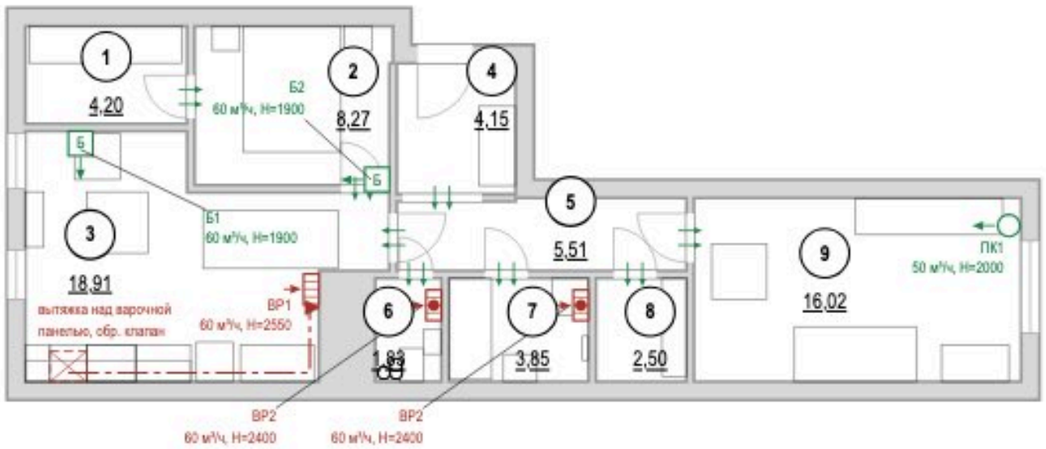

Примечания

1. Расчёт систем ОВ и подбор оборудования — проектная организация с допуском СРО; лист даёт места, трассы и привязки.
2. Нормы вытяжки — СП 54.13330.2022 (Изм. 1, 2), табл. 7.1: кухня с электроплитой 60 м³/ч, с газовой 100; ванная и совмещённый санузел 50; уборная 25; гардеробная 0,2 ч⁻¹. Приток в жилые — 3 м³/ч на 1 м² (менее 20 м² общей площади на человека), иначе 30 м³/ч на человека.
3. Вентканалы и шахты не сужать, не переносить и не закрывать; вентилятор и кухонная вытяжка — через обратный клапан, без перекрытия естественной тяги.
4. Проектные расходы — не ниже нормы, вытяжка сведена с притоком вентиляторами мокрых помещений. Клапаны — в простенке у окна, центр 2000 мм, не над кроватью, не ближе 300 мм к стоякам отопления; типоразмер — на расход.
5. Кухонная вытяжка в воздухообмен не включена: воздуховод не менее Ø125 в коробе, вход в канал отдельный.
6. Переток — зазор под полотнами межкомнатных дверей или переточная решётка.
7. Кондиционирование заданием не предусмотрено; при установке трассы фреона и дренажа (не менее 40 мм/м, в К1 через сифон) и питание заложить до черновых работ.
8. Привязки оборудования — по паспортам приобретённых моделей, до черновых работ.

Условные обозначения

- стояк: К1 — канализация, В1 — ХВС, Т3 — ГВС
- 1 — номер помещения, площадь м²
- вытяжная решётка в вентканал: марка, расход м³/ч, Н центра от чистого пола
- вытяжная решётка с бытовым вентилятором и обратным клапаном: марка, расход, Н
- приточный клапан (КИВ) в наружной стене: марка, расход, Н центра
- Б — бризер (приток с фильтром и подогревом)
- переток: зазор под полотном или переточная решётка
- кухонная вытяжка над варочной панелью
- воздуховод кухонной вытяжки в коробе под потолком
- отдельный вход воздуховода в вентканал, обратный клапан

Воздухообмен, м³/ч

№	Помещение	Выт. норма	Выт. проект	Прит. норма	Прит. проект	Устройства
1	Гардеробная	2				переток
2	Спальня			60	60	Б2
3	Кухня-гостиная	60	60	60	60	ВР1, Б1
6	Санузел	25	60			ВР2
7	Ванная	50	60			ВР2
8	Кладовая	1				переток
9	Детская			49	50	ПК1
	Итого	**138**	**180**	**60**	**170**	

Воздухообмен квартиры — по большей из сумм притока и вытяжки: норма 138 м³/ч, проект 180 м³/ч.
Вытяжка не меньше притока — баланс сведён.

Допущения и предложения на листе

Основа листа: размеры сняты с растрового плана заказчика без размеров: масштаб восстановлен по площадям помещений (≈ 11,8 мм на пиксель), контрольный обмер не выполнен (К-1); высота потолка 2700 мм принята: на плане заказчика её нет (К-2); толщины стен 300 / 120 мм приняты по плану заказчика, не замерены (К-1); разрешённая мощность 15 кВт принята по типовым ТУ для квартиры, ТУ заказчиком не переданы (К-4).
См. лист открытых вопросов (лист 5, записи К-1, К-2, К-4).

1000 мм · печать 1:1

Изм.	Кол.уч	Лист	№ док.	Подп.	Дата
Разраб.		Кырпан А.С.			09.10.26
Пров.					
ГИП					
Н. контр.					
Утв.					

ГД-2026-007-АИ

Квартира 65 м²

Общая площадь 65,24* м² · * размеры со скана, не замерены (реестр — п. 5, К-1)

Дизайн-проект интерьера

Стадия	Лист	Листов
РП	25	79

План вентиляции

М 1:100


Кырпан Александр Сергеевич

выпуск 09.10.2026 № 147dabfd23 · стр. 31 из 110

План отопления

Радиаторы, стояки, подводки · размеры в мм · высоты от чистого пола

ПРЕДВАРИТЕЛЬНО · не для производства работ · открыто пунктов: 4 (реестр — л. 5)

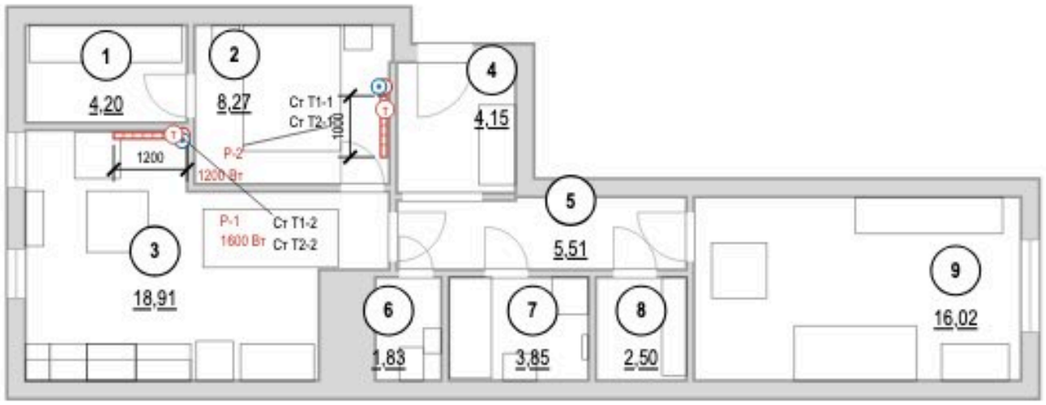

Условные обозначения

- (1) — номер помещения, площадь м²
- радиатор отопления (марка РО-N, длина по плану)
- (T) — клапан с термоголовкой на подаче
- стояк отопления, подающий (Ст Т1-N)
- стояк отопления, обратный (Ст Т2-N)
- Т1 — отопление, подающий трубопровод
- Т2 — отопление, обратный трубопровод

Ведомость радиаторов

Марка	Помещение	Тип	Д×В×Г, мм	Низ / стена	Q, Вт
P-2	2. Спальня	панельный 22	1000×500×100	120 / 40	1200
P-1	3. Кухня-гостиная	панельный 22	1200×500×100	120 / 40	1600

Низ — от чистого пола, стена — зазор до задней панели, мм.

Привязки — до обмера

Стояки отопления в исходных данных не заданы: показаны у откосов окон, подводки — принципиально. До черновых работ — обмер стояков и паспорта приборов; лист перевыпустить по факту.

Примечания

1. Расчёт системы отопления, теплопотерь и подбор приборов — проектная организация с допуском СРО; лист даёт места и привязки.
2. Тип, длина и мощность радиаторов — по теплотехническому расчёту; лист задаёт места, зазоры и подключение.
3. Зазоры радиатора: низ не менее 100 мм от чистого пола, верх не менее 100 мм до подоконника, 30–50 мм от стены до задней панели; центр по оси окна с допуском ±20 мм.
4. Радиаторы не закрывать глухими коробами и мебелью; перенос и замена приборов в многоквартирном доме — переустройство, согласование с управляющей организацией (ЖК РФ ст. 25–26); вынос на лоджию запрещён.
5. Трубы отопления через межквартирные стены не прокладывать (СП 51.13330.2011, п. 9.19); через перекрытия и перегородки — в гильзах.
6. Привязки приборов и подводок — по паспортам приобретённых радиаторов и клапанов, до черновых работ.
7. До закрытия отделкой трубопроводы отопления испытать гидростатическим давлением с оформлением акта (СП 73.13330.2016, 7.2–7.3).

Допущения и предложения на листе

Основа листа: размеры сняты с растрового плана заказчика без размеров: масштаб восстановлен по площадям помещений (≈ 11,8 мм на пиксель), контрольный обмер не выполнен (К-1); высота потолка 2700 мм принята: на плане заказчика её нет (К-2); толщины стен 300 / 120 мм приняты по плану заказчика, не замерены (К-1); разрешённая мощность 15 кВт принята по типовым ТУ для квартиры, ТУ заказчиком не переданы (К-4).

См. лист открытых вопросов (лист 5, записи К-1, К-2, К-4).

1000 мм · печать 1:1

Изм.	Кол.уч	Лист	№ док.	Подп.	Дата
Разраб.		Кырлан А.С.			09.10.26
Пров.					
ГИП					
Н. контр.					
Утв.					

ГД-2026-007-АИ

Квартира 65 м²

Общая площадь 65,24* м² · * размеры со скана, не замерены (реестр — п. 5, К-1)

Дизайн-проект интерьера	Стадия	Лист	Листов
	РП	26	79

План отопления

М 1:100

Кырлан Александр Сергеевич

выпуск 09.10.2026 № 147dabfd23 · стр. 32 из 110

05

Водоснабжение и канализация

Кырлан Александр Сергеевич


выпуск 09.10.2026 № 147dabfd23 · стр. 33 из 110

План выводов сантехники


Выводы В1, Т3, К1 · привязки от чистовых стен · высоты от чистого пола, мм

ПРЕДВАРИТЕЛЬНО · не для производства работ · открыто пунктов: 4 (реестр — л. 5)


Фрагмент 1. Кухня-гостиная (пом. 3)

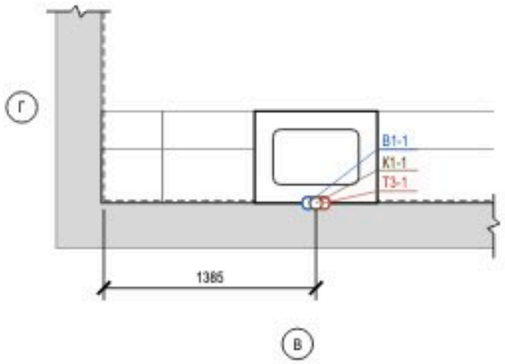

Фрагмент 2. Санузел (пом. 6)

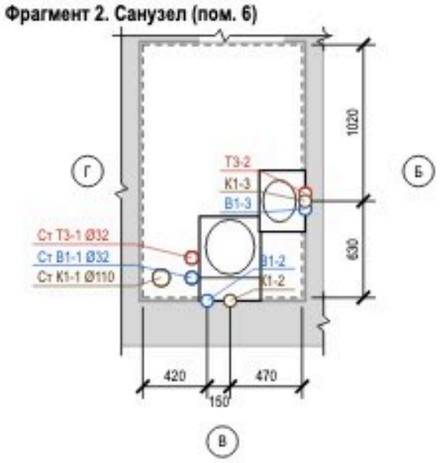

Фрагмент 3. Ванная (пом. 7)

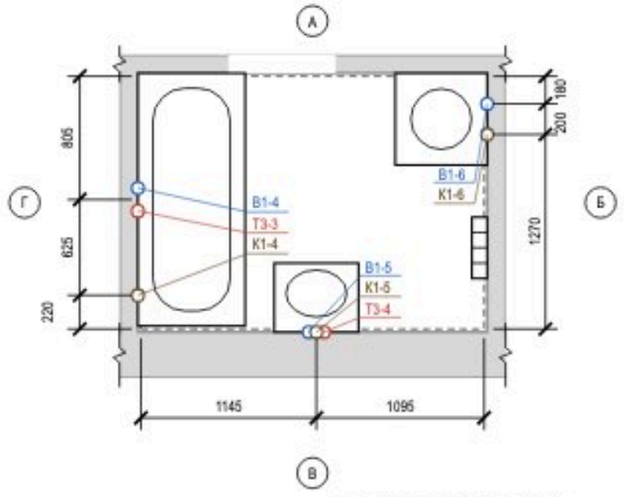

Ведомость привязок выводов

Код	Прибор	Ø	H, мм	Привязка от чист. стен, мм	Прим.
В1-1	П4 мойка кухонная	½"	550	ст. В: 1335 от Г	межос. 100
Т3-1	П4 мойка кухонная	½"	550	ст. В: 1435 от Г	межос. 100
К1-1	П4 мойка кухонная	Ø50	400	ст. В: 1385 от Г	
В1-2	П20 унитаз подвесной	½"	1000	ст. В: 420 от Г	в раме инсталляции
К1-2	П20 унитаз подвесной	Ø110	220	ст. В: 470 от Б	
В1-3	П21 умывальник	½"	550	ст. Б: 680 от В	межос. 100
Т3-2	П21 умывальник	½"	550	ст. Б: 680 от В	межос. 100
К1-3	П21 умывальник	Ø50	500	ст. Б: 630 от В	
В1-4	П1 ванна	½"	800	ст. Г: 730 от А	межос. 150
Т3-3	П1 ванна	½"	800	ст. Г: 770 от В	межос. 150
К1-4	П1 ванна	Ø50	50	ст. Г: 220 от В	
В1-5	П3 умывальник	½"	550	ст. В: 1095 от Г	межос. 100
Т3-4	П3 умывальник	½"	550	ст. В: 1045 от Б	межос. 100
К1-5	П3 умывальник	Ø50	500	ст. В: 1095 от Б	
В1-6	П22 стиральная машина	½"	800	ст. Б: 180 от А	кран машины
К1-6	П22 стиральная машина	Ø50	600	ст. Б: 380 от А	

* — высота по практике монтажа; сверить по паспорту прибора

Условные обозначения

- вывод В1 (код — в ведомости привязок)
- вывод Т3 (код — в ведомости привязок)
- вывод К1 (код — в ведомости привязок)
- сантехприбор по расстановке (габарит модели)
- чистовая поверхность стены (от неё привязки)
- стояк «Ст К1-N / Ст В1-N» (ГОСТ 21.601), Ø мм
- линия обрыва (граница фрагмента)
- обозначение стены А–Г (как на развёртках)

Допущения и предложения на листе

Основа листа: размеры сняты с растрового плана заказчика без размеров: масштаб восстановлен по площадям помещений (≈ 11,8 мм на пиксель), контрольный обмер не выполнен (К-1); высота потолка 2700 мм принята: на плане заказчика её нет (К-2); толщины стен 300 / 120 мм приняты по плану заказчика, не замерены (К-1); разрешённая мощность 15 кВт принята по типовым ТУ для квартиры, ТУ заказчиком не переданы (К-4).
См. лист открытых вопросов (лист 5, записи К-1, К-2, К-4).

Примечания

1. Привязки выводов даны от чистовых поверхностей стен (облицовка на сторону: кухня-гостиная — 15 мм (по данным); санузел — 20 мм (по данным); ванная — 20 мм (по данным)); эти же грани — на развёртках и в раскладке плитки. Высоты — от чистого пола помещения.
2. Высоты и межосевые, отмеченные «*», приняты по практике монтажа; до черновой разводки сверить по паспорту выбранного прибора (смеситель, инсталляция, сифон).
3. Горячая вода (Т3) — слева от холодной (В1), если смотреть на прибор. Допуск установки выводов: ±5 мм в группе, ±20 мм у отдельно стоящих.
4. Расчёт систем водоснабжения и канализации и подбор оборудования выполняет проектная организация; лист задаёт места и высоты выводов.

1000 мм · печать 1:1

Изм.	Кол.уч	Лист	№ док.	Подп.	Дата
Разраб.		Кырпан А.С.			09.10.26
Пров.					
ГИП					
Н. контр.					
Утв.					

ГД-2026-007-АИ

Квартира 65 м²

Общая площадь 65,24* м² · * размеры со скана, не замерены (реестр — п. 5, К-1)

Дизайн-проект интерьера

Стадия	Лист	Листов
РП	27	79

План выводов сантехники

М 1:40


Кырпан Александр Сергеевич

выпуск 09.10.2026 · 147dabfd23 · стр. 34 из 110


Схема разводки водопровода и канализации

Схемы систем В1, Т3, К1 · трассы принципиальные · уклоны в мм на 1 м · план М 1:400, фрагменты М 1:25


План квартиры (М 1:400)

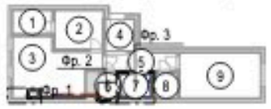


Фр. 1. Кухня-гостиная (М 1:25)

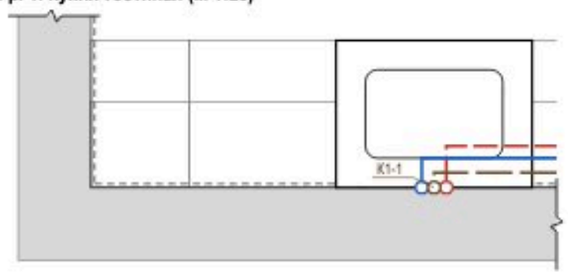

Фр. 2. Санузел (М 1:25)

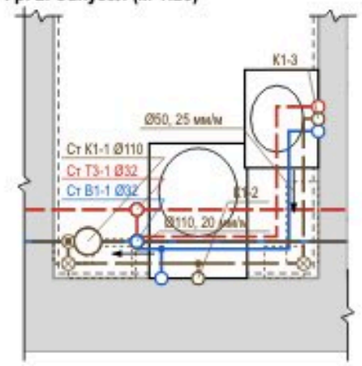

Фр. 3. Ванная (М 1:25)

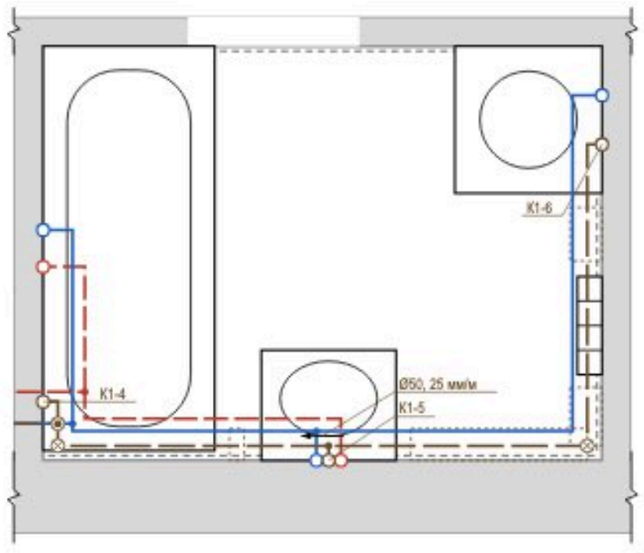

Условные обозначения

- В1 — водопровод хозяйственно-питьевой (ХВС), PP-R Ø20
- Т3 — горячее водоснабжение, подача (ГВС), PP-R Ø20
- К1 — канализация бытовая
- направление уклона К1 / пола: Ø, мм на 1 м
- ⊗ ревизия (прочистка) К1 — доступ сохранить
- • тройник (ответвление к прибору)
- короб К1 над чистым полом (ГКЛВ под плитку)
- ○ вывод В1 (код — в ведомости привязок)
- ○ вывод Т3 (код — в ведомости привязок)
- ○ вывод К1 (код — в ведомости привязок)
- сантехприбор по расстановке (габарит модели)
- ○ стояк «Ст К1-N / Ст В1-N» (ГОСТ 21.601), Ø мм
- линия обрыва (граница фрагмента)
- граница фрагмента на плане (Фр. N)

Профиль выпусков К1 (до врезки в стояк)

Выпуск	Прибор	Ø	L, м	i, мм/м	Δh, мм	Прокладка, мм
К1-2	П20 унитаз подвесной	Ø110	0,76	20	15	короб 160×140
К1-6	П22 стиральная машина	Ø50	4,66	25	117	короб 200×110
К1-1	П4 мойка кухонная	Ø50	4,60	25	115	над полом за приборами
К1-5	П3 умывальник	Ø50	2,38	25	59	над полом за приборами
К1-3	П21 умывальник	Ø50	1,78	25	45	короб 130×110
К1-4	П1 ванна	Ø50	1,27	25	32	в полу: нужно 157 > 90 — решение!

Короб h×b: h — от чистого пола, b — от чистовой стены. Стяжка 90 мм — лист полов.

Узел ввода В1, Т3 (схема, без масштаба)



⊗ Ст К1-1: ревизия на стояке — люк в коробе

Допущения и предложения на листе

Основа листа: размеры сняты с растрового плана заказчика без размеров: масштаб восстановлен по площадям помещений (≈ 11,8 мм на пиксель), контрольный обмер не выполнен (К-1); высота потолка 2700 мм принята: на плане заказчика её нет (К-2); толщины стен 300 / 120 мм приняты по плану заказчика, не замерены (К-1); разрешённая мощность 15 кВт принята по типовым ТУ для квартиры, ТУ заказчиком не переданы (К-4).
См. лист открытых вопросов (лист 5, записи К-1, К-2, К-4).

Примечания

1. Трассы принципиальные, построены от стояков вдоль стен помещений; фактическое положение фиксируется исполнительной схемой с привязками (фото с рулеткой) до закрытия.
2. Уклон К1 не менее 1/d и не более 150 мм/м (СП 30.13330.2020, п. 19.1), приняты практические уклоны; поворот — двумя отводами 45°, ревизия после поворота, доступ сохранить. Стояк К1 в коробе — звукоизоляция стояка в коробе, без жёсткого контакта короба с трубой.
3. Решение по К1: стяжка 90 мм не укрывает трубы (нужно Ø + Δh + 45 мм) — выпуски идут над чистым полом вдоль стен: К1-1, К1-5 — за приборами и в раме инсталляции; К1-2, К1-6, К1-3 — в коробе ГКЛВ под плитку (размеры в профиле). Короба — на развёртках; отметку низа врезки в стояк замерить до черновых работ.
4. На каждом вводе В1 и Т3 — кран шаровой, фильтр, счётчик, обратный клапан; доступ через люк не меньше 300×400. Водопровод — в штробе стен или в коробах; трубы испытать давлением до закрытия (акт скрытых работ).
5. Расчёт систем, диаметры магистралей и подбор оборудования выполняет проектная организация; врезка и перенос стояков — по согласованию с управляющей организацией. Арматуру и привязки сверить по паспортам приборов.

Изм.	Кол.уч	Лист	№ док.	Подп.	Дата	ГД-2026-007-АИ			
						Квартира 65 м²			
						Общая площадь 65,24* м² · * размеры со скана, не замерены (реестр — п. 5, К-1)			
Разраб.		Кырлан А.С.			09.10.26	Дизайн-проект интерьера	Стадия	Лист	Листов
Пров.							РП	28	79
ГИП									
Н. контр.						Схема разводки водопровода и канализации	Кырлан Александр Сергеевич		
Утв.						М 6/м			

выпуск 09.10.2026 · 147dabfd23 · стр. 35 из 110

Спецификация сантехнического оборудования

Форма 1 ГОСТ 21.110-2013 · ГД-2026-007-АИ-ВК.СО · приборы, арматура, трубопроводы

ПРЕДВАРИТЕЛЬНО · не для производства работ · открыто пунктов: 4 (реестр — л. 5)

Поз.	Наименование и техническая характеристика	Тип, марка, обозначение документа	Код продукции	Поставщик	Ед. изм.	Кол.	Масса 1 ед., кг	Примечание
	Санитарные приборы							
1	Ванна акриловая 1650×700 мм, с каркасом, экраном и отверстием слив-перелив	Ravak Classic C541000000		выбор заказчика	шт	1		П1
2	Унитаз подвесной безободковый, с сиденьем микролифт, крепёж и звукоизолирующая прокладка	Jacob Delafon Struktura EDF102-00		выбор заказчика	шт	1		П20
3	Инсталляция для подвесного унитаза: рама высотой 1120 мм, бачок, клавиша смыва (ось клавиши 1050 мм от чистого пола)	аналог		выбор заказчика	шт	1		П20; короб ГКЛВ
4	Умывальник подвесной 400×300 мм, с отверстием под смеситель и переливом	Roca The Gap 7.3274.7.400.0		выбор заказчика	шт	1		П21
5	Умывальник подвесной 550×450 мм, с отверстием под смеситель и переливом	Roca The Gap 7.3274.7.400.0		выбор заказчика	шт	1		П3
6	Мойка кухонная 800×600 мм, с переливом	мойка врезная 780×510 в шкафу М6		с кухонной мебелью	шт	1		П4
7	Полотенцесушитель электрический, IP44, с терморегулятором	аналог		выбор заказчика	шт	1		П5
	Смесители, сифоны и арматура приборов							
8	Смеситель для ванны настенный однорычажный, межосевое 150 мм, с душевым набором (лейка, шланг, держатель)	аналог		выбор заказчика	шт	1		П1
9	Смеситель для умывальника однорычажный, с донным клапаном	аналог		выбор заказчика	шт	2		П21, П3
10	Смеситель кухонный однорычажный, высокий излив	аналог		выбор заказчика	шт	1		П4
11	Обвязка ванны слив-перелив Ø40/50 с сифоном	аналог		выбор заказчика	шт	1		П1
12	Сифон для умывальника бутылочный Ø32/40–50, с гофрой к выпуску	аналог		выбор заказчика	шт	2		П21, П3
13	Сифон для мойки Ø40/50	аналог		выбор заказчика	шт	1		П4
14	Сифон для стиральной машины встраиваемый в стену Ø50, с обратным клапаном	аналог		выбор заказчика	шт	1		П22
15	Кран угловой ½"×½" с гибкой подводкой 40 см (умывальники, мойка)	аналог		выбор заказчика	шт	6		по 2 на прибор
16	Кран шаровой угловой ½"×¾" для подключения стиральной и посудомоечной машины	аналог		выбор заказчика	шт	1		П22
	Трубопроводы							
17	Труба полипропиленовая PP-R PN20 Ø20×3,4 (В1)	ГОСТ 32415-2013		выбор заказчика	м	18	0,17	11,8 + 4,3 + 10 %
18	Труба PP-R, армированная стекловолокном, PN20 Ø20×2,8 (Т3)	ГОСТ 32415-2013		выбор заказчика	м	13	0,15	9,3 + 2,5 + 10 %
19	Труба канализационная ПП Ø50 (К1)	ГОСТ 32414-2013		выбор заказчика	м	14		10,5 + 2,0 + 10 %
20	Труба канализационная ПП Ø110 (К1)	ГОСТ 32414-2013		выбор заказчика	м	1,5		0,8 + 0,2 + 10 %
	Фасонные части и выводы							
21	Отвод канализационный ПП 45° Ø50	ГОСТ 32414-2013		выбор заказчика	шт	20		2 шт. на поворот
22	Отвод канализационный ПП 45° Ø110	ГОСТ 32414-2013		выбор заказчика	шт	6		2 шт. на поворот
23	Тройник канализационный ПП 45° (врезки ветвей)	ГОСТ 32414-2013		выбор заказчика	шт	5		
24	Ревизия канализационная ПП (после поворота трассы)	ГОСТ 32414-2013		выбор заказчика	шт	8		доступ сохранить
25	Фитинги PP-R Ø20: тройники, угольники 90° (ветви и повороты В1, Т3)	ГОСТ 32415-2013		выбор заказчика	шт	29		
26	Водорозетка PP-R Ø20×½" настенная, с креплением	ГОСТ 32415-2013		выбор заказчика	шт	10		коды — лист выводов
	Узлы ввода, люки, короба							
27	Кран шаровой латунный Ду15 PN16 (отключение ввода)	аналог		выбор заказчика	шт	2		Ст В1-1, Ст Т3-1
28	Фильтр сетчатый косой Ду15	аналог		выбор заказчика	шт	2		
29	Счётчик воды крыльчатый Ду15 (ХВ, ГВ), с поверкой	аналог		выбор заказчика	шт	2		пломба УК
30	Клапан обратный Ду15	аналог		выбор заказчика	шт	2		
31	Люк ревизионный накимной под плитку 300×400 мм	аналог		выбор заказчика	шт	1		к стоякам и арматуре
32	Звукоизоляция стояка К1 в коробе: рулонный звукоизоляционный материал ≥ 10 мм, обмотка стояка на высоту этажа	аналог		выбор заказчика	м	2,7		Ст К1-1
33	Короб К1 над полом: профиль ПНПС, ГКЛВ 12,5 мм под плитку	аналог		выбор заказчика	м	2,9		сечение — лист разводки

Примечания

1. Форма 1 ГОСТ 21.110-2013, ширины граф изменены по п. 4.1. «Аналог» — аналог по характеристикам: модели внести до чертежных работ, привязки выводов сверить по паспортам.
2. Бытовая техника не входит (показана арматура подключения), мойка — в комплекте кухни. Длины труб — трасса листа разводки + подъёмы + 10 %.
3. Стояк К1 в коробе — звукоизоляция стояка в коробе без жёсткого контакта короба с трубой.
4. Расчёт систем водоснабжения и канализации, диаметры магистралей и подбор оборудования выполняет проектная организация.

Допущения и предложения на листе

Основа листа: размеры сняты с растрового плана заказчика без размеров: масштаб восстановлен по площадям помещений (≈ 11,8 мм на пиксель), контрольный обмер не выполнен (К-1); высота потолка 2700 мм принята: на плане заказчика её нет (К-2); толщины стен 300 / 120 мм приняты по плану заказчика, не замерены (К-1); разрешённая мощность 15 кВт принята по типовым ТУ для квартиры, ТУ заказчиком не переданы (К-4).
См. лист открытых вопросов (лист 5, записи К-1, К-2, К-4).

Изм.	Кол.уч	Лист	№ док.	Подп.	Дата	ГД-2026-007-АИ		
						Квартира 65 м²		
						Общая площадь 65,24* м² · * размеры со скана, не замерены (реестр — п. 5, К-1)		
Разраб.		Кырпан А.С.			09.10.26	Дизайн-проект интерьера	Стадия: РП	Лист: 29 / Листов: 79
Пров.								
ГИП								
Н. контр.						Спецификация сантехнического оборудования	Кырпан Александр Сергеевич	
Утв.						М 6/м		

выпуск 09.10.2026 · 147dabfd23 · стр. 36 из 110

Спецификация светильников и сценарии освещения

Светильники, ленты и блоки питания, слои света и сценарии по помещениям · б/м

Спецификация светильников

Поз.	Марки	Наименование	Установка	Кол.	P, Вт	Σ P, Вт	Ф, лм	Tц, K	Ra	Угол, °	IP	Дим.	Группа	Пом.
1	Св16	Потолочный накладной	на потолке, засветка стены	1	10	10	900	3000	90	—	20	—	L6	1
2	Св1	Потолочный накладной	на потолке	1	36	36	3200	2700	90	—	20	—	L2	2
3	Св5*	Трековая система	на потолке	2	12	24	900	2700	90	—	20	—	L2	2
4	Св2, Св3	Настенный (бра)	на стене, H=1300	2	4	8	250	2700	90	—	20	—	L8	2
5	Св4	Подвесной	подвес	1	24	24	2400	3000	90	—	20	—	L1	3
6	Св6	Потолочный накладной	на потолке	1	18	18	1800	3000	90	—	20	—	L1	3
7	Св7	Потолочный накладной	на потолке	1	12	12	1100	3000	90	—	20	—	L1	3
8	Св8	Потолочный накладной	на потолке	1	12	12	1000	4000	90	—	20	—	L1	3
9	Св9	Линейный настенный	под верхними шкафами, H=1400	1	18	18	1300	3000	90	—	20	—	L6	3
10	Св10–Св12	Встраиваемый точечный	встраиваемый	3	9	27	800	3000	90	—	20	—	L3	4, 5
11	Св13	Встраиваемый точечный	встраиваемый	1	6	6	500	3000	90	—	20	—	L4	6
12	Св14	Встраиваемый точечный	встраиваемый	1	9	9	700	3000	90	—	44	—	L4	7
13	Св15	Настенный (бра)	над зеркалом, H=1900	1	6	6	400	3000	90	—	44	—	L4	7
14	Св26	Потолочный накладной	на потолке	1	9	9	600	3000	90	—	20	—	L3	8
15	Св17–Св22	Встраиваемый точечный	встраиваемый	6	12	72	1050	2700	90	—	20	—	L7	9
16	Св23	Лента светодиодная 24 В	в коробе, профиль с рассеивателем	12,3 м	9,6/м	118,1	900/м	2700	90	—	20	да	L8	9
17	Св24, Св25	Настенный (бра)	на стене, H=1500	2	6	12	400	2700	90	60	20	—	L9	9
		Итого		**26 шт + 12,3 м**		**421,1**								

LED-ленты, линейные светильники и блоки питания

Марка	Пом.	L, м	U, В	Вт/м	Σ P, Вт	БП	P БП, Вт	Загр., %	Питание	Доступ к БП
Св9*	2	0,8	24	—	24	БП2	200	71	встроенный ввод	люк 300×300 в коробе У1 у окна
—	3	2,5	24	—	18	БП1	60	30	встроенный ввод	H=2300
Св23	9	12,3	24	9,6	118,1	БП2	200	71	с двух концов	люк 300×300 в коробе У1 у окна

Сценарии освещения

Пом.	Сценарий	Группы и уровни, %	Чем включается
9	Вечер	L7 споты — 0; L8 подсветка короба — 100; L9 бра — 100	S4, S5, S6

Слои света

общий — равномерный свет помещения, по норме освещённости

рабочий — местный свет задачи: столешница, зеркало, чтение у кровати

акцентный — подсветка потолка, стен и ниш; не входит в поток общего света

Слои света по помещениям

Пом.	Помещение	Слои света и группы включения (марки светильников)	Tц, K	Ra	Σ P, Вт	Сцен.
1	Гардеробная	общий — L6 (Св16)	3000	90	10	—
2	Спальня	общий — L2 (Св1, Св5**); рабочий — L8 (Св2, Св3)	2700	90	68	—
3	Кухня-гостиная	общий — L1 (Св4, Св6–Св8); рабочий — L6 (Св9)	3000 / 4000	90	84	—
4	Прихожая	общий — L3 (Св10)	3000	90	9	—
5	Коридор	общий — L3 (Св11, Св12)	3000	90	18	—
6	Санузел	общий — L4 (Св13)	3000	90	6	—
7	Ванная	общий — L4 (Св14); рабочий — L4 (Св15)	3000	90	15	—
8	Кладовая	общий — L3 (Св26)	3000	90	9	—
9	Детская	общий — L7 (Св17–Св22); рабочий — L9 (Св24, Св25); акцентный — L8 (Св23)	2700	90	202,1	1

Допущения и предложения на листе

Основа листа: размеры сняты с растрового плана заказчика без размеров: масштаб восстановлен по площадям помещений (≈ 11,8 мм на пиксель), контрольный обмер не выполнен (К-1); высота потолка 2700 мм принята: на плане заказчика её нет (К-2); толщины стен 300 / 120 мм приняты по плану заказчика, не замерены (К-1); разрешённая мощность 15 кВт принята по типовым ТУ для квартиры, ТУ заказчиком не переданы (К-4).

Знак «**» — предложение проектировщика, заказчиком не утверждено (согласовать с заказчиком): записи в реестре нет: Св5 — трековая система 2 × 900 лм: светильник добавлен проектировщиком, поток принят до нормы освещённости, модель и паспорт не выбраны.

См. лист открытых вопросов (лист 5, записи К-1, К-2, К-4).

Примечания

1. Позиции и марки Св — те же, что на плане освещения (лист 19) и в ведомости светильников (лист 21); группы L — по плану выключателей (лист 20).
2. Модели светильников не назначены: подбор по графам спецификации — поток, Tц, Ra, угол, IP и диммирование не хуже указанных, мощность не больше. IP 20 — сухие помещения.
3. Длина LED-ленты в карнизе — по линии карниза плана потолков (лист 31); Σ P = Вт/м × длина. Блок питания загружен не больше чем на 80 %; лента 24 В длиннее 10 м питается с двух концов; доступ к блоку питания — люк ревизии 300×300 мм или место, указанное в таблице.
4. Сценарии: уровень — доля максимальной яркости группы, %; 0 — группа выключена. Уровень ниже 100 % — только у групп на светорегуляторе (задний фронт, ТЕ) с диммируемыми драйверами и блоками питания.
5. Мощность и поток — по паспортам принятых изделий, Σ P — установленная мощность освещения. Оценка освещённости — на плане освещения; это не светотехнический расчёт.

Изм.	Кол.уч	Лист	№ док.	Подп.	Дата	ГД-2026-007-АИ			
						Квартира 65 м²			
						Общая площадь 65,24* м² · * размеры со скана, не замерены (реестр — п. 5, К-1)			
Разраб.		Кырпан А.С.			09.10.26	Дизайн-проект интерьера	Стадия	Лист	Листов
Пров.							РП	30	79
ГИП									
Н. контр.						Спецификация светильников и сценарии освещения М б/м	Кырпан Александр Сергеевич		
Утв.									

выпуск 09.10.2026 № 147dabfd23 · стр. 37 из 110

06

Потолки и ГКЛ-конструкции

Кырлан Александр Сергеевич

выпуск 09.10.2026 № 147dabfd23 · стр. 38 из 110

План потолков

Уровни и марки потолков, короба с подсветкой, ниши под шторы, люки, вырезы · отметки низа от ±0,000 чистого пола · размеры в мм



ПРЕДВАРИТЕЛЬНО · не для производства работ · открыто пунктов: 4 (реестр — л. 5)

Ведомость потолков

Пом.	Марка	Конструкция	Низ	S, м²	Q
1		по плите, окраска	+2,700	4,20	
2		по плите, окраска	+2,700	8,27	
3		по плите, окраска	+2,700	18,91	
4		по плите, окраска	+2,700	4,15	
5		по плите, окраска	+2,700	5,51	
6		по плите, окраска	+2,700	1,83	
7		по плите, окраска	+2,700	3,85	
8		по плите, окраска	+2,700	2,50	
9		по плите, окраска	+2,700	16,02	
		Итого		**65,24**	

Ведомость вырезов и закладных в потолке

Марка	Устройство	Кол.	Пом.
	Светильник встраиваемый (марки — план освещения)	11	4, 5, 6, 7, 9
	Светильник накладной (марки — план освещения)	6	1, 2, 3, 8
	Светильник подвесной (марки — план освещения)	1	3
ИП2	Извещатель дымовой	3	2, 3, 9

Условные обозначения

- потолок по плите перекрытия, окраска, низ +2,700
- светильник накладной — подложка с плана освещения
- светильник подвесной — подложка с плана освещения
- светильник встраиваемый — подложка с плана освещения
- Д — извещатель дымовой на потолке — подложка
- +2,6 — отметка низа потолка, м; под ней марка потолка
- новое — возводится по проекту (синим)
- 1 — номер помещения, площадь м²

Примечания

1. За отметку ±0,000 принят уровень чистого пола сухих помещений (готовое покрытие), а не существующего пола; пол пом. 6, 7 — −0,015; верх плиты перекрытия −0,064 — расчётный по пирогу пола, не замерен; существующий пол снимается до плиты, его отметка не замерена. Отметки в прямоугольниках — низ потолка; низ плиты перекрытия +2,700. Марка потолка — одна конструкция и отметка на весь альбом.
2. Светильники и потолочные устройства — подложка с планов освещения, слаботочных систем и вентиляции (положение — по ним); вырезы и закладные — по ведомости на листе, до обшивки; отверстия не совмещать с профилями.
3. Пом. 1, 2, 3, 4, 5, 6, 7, 8, 9 — потолок по плите без подвесной системы; отделка — по ведомости отделки.

Допущения и предложения на листе

Основа листа: размеры сняты с растрового плана заказчика без размеров: масштаб восстановлен по площадям помещений (≈ 11,8 мм на пиксель), контрольный обмер не выполнен (К-1); высота потолка 2700 мм принята: на плане заказчика её нет (К-2); толщины стен 300 / 120 мм приняты по плану заказчика, не замерены (К-1); разрешённая мощность 15 кВт принята по типовым ТУ для квартиры, ТУ заказчиком не переданы (К-4). Открытые вопросы и конфликты по листу: К-2.

См. лист открытых вопросов (лист 5, записи К-1, К-2, К-4).

1000 мм · печать 1:1

Изм.	Кол.уч	Лист	№ док.	Подп.	Дата
Разраб.		Кырпан А.С.			09.10.26
Пров.					
ГИП					
Н. контр.					
Утв.					

ГД-2026-007-АИ

Квартира 65 м²

Общая площадь 65,24* м² · * размеры со скана, не замерены (реестр — л. 5, К-1)

Дизайн-проект интерьера	Стадия	Лист	Листов
	РП	31	79

План потолков

М 1:100

Кырпан Александр Сергеевич

выпуск 09.10.2026 · 147dabfd23 · стр. 39 из 110

Раскладка плитки. Планы полов

ПРЕДВАРИТЕЛЬНО · не для производства работ · открыто пунктов: 4 (реестр — л. 5)

Раскладка от чистовых размеров · размеры в мм · отметки от ±0,000

Ведомость плитки

Помещение, поверхность	Плитка, код	Формат	Шов	S, м²	Целых	Подр.	С запасом
Прихожая, пол	SG501600R	600×1200	2	4,15	0	8	9
Коридор, пол	SG501600R	600×1200	2	5,51	0	8	9
Санузел, пол	SG501600R	600×1200	2	1,83	0	4	5
Ванная, пол	SG501600R	600×1200	2	3,85	0	8	9
Итого 600×1200				**15,34**	**0**	**28**	**32**

Ведомость материалов

Материал	Класс, код	Норма расхода	Кол-во
Затирка	класс не задан	(a+b)/ab·шов·1,6	1,2 кг
Клей	C2	1,5 кг/м²·мм, слой 5	79 кг (4 меш.)
Клей	C2 S1	1,5 кг/м²·мм, слой 5	46 кг (2 меш.)
Демпф. лента	по периметру пола из плитки		27,2 м

Условные обозначения

- плитка целая; тонкая линия — шов
- плитка с подрезкой (размер — на цепочке)
- ось старта; стрелки — направление укладки
- сантехприбор: габарит, высота по практике
- отметка чистого пола на полке выноски, м
- (А) обозначение стены А–Г (как на развёртках)

Примечания

1. Плитка пола мокрых помещений не задана — планы полов санузлов не выполнены; на листе — ведомость плитки остальных помещений.
2. Толщины облицовки стен не заданы: раскладка от черновых размеров, до укладки пересчитать от чистовых.
3. Раскладка пола «Прихожая» и пола «Коридор» и пола «Санузел» и пола «Ванная» — на листе «Раскладка плитки. Прихожая. Коридор. Санузел. Ванная».
4. Калибр партии не задан — до укладки замерить (рабочий размер W, ГОСТ 13996-2019) и пересчитать подрезки.
5. Количество: целые по раскладке + по одной на подрезку, запас 10 %; один артикул — одна партия и тон. Исключены поддон, короб, проёмы и места за коробом; S — по чистым граням, как в ведомости отделки.
6. Клей С2; С2 S1 (ГОСТ Р 56387-2018), затирка класс не задан; расход — по ТУ выбранной марки.

Допущения и предложения на листе

Основа листа: размеры сняты с растрового плана заказчика без размеров: масштаб восстановлен по площадям помещений (≈ 11,8 мм на пиксель), контрольный обмер не выполнен (К-1); высота потолка 2700 мм принята: на плане заказчика её нет (К-2); толщины стен 300 / 120 мм приняты по плану заказчика, не замерены (К-1); разрешённая мощность 15 кВт принята по типовым ТУ для квартиры, ТУ заказчиком не переданы (К-4).

См. лист открытых вопросов (лист 5, записи К-1, К-2, К-4).

1000 мм · печать 1:1

Изм.	Кол.уч	Лист	№ док.	Подп.	Дата
Разраб.		Кырлан А.С.			09.10.26
Пров.					
ГИП					
Н. контр.					
Утв.					

ГД-2026-007-АИ

Квартира 65 м²

Общая площадь 65,24* м² · * размеры со скана, не замерены (реестр — п. 5, К-1)

Дизайн-проект интерьера	Стадия	Лист	Листов
	РП	32	79

Раскладка плитки. Планы полов

М 1:20

Кырлан Александр Сергеевич


выпуск 09.10.2026 · 147dabfd23 · стр. 40 из 110

Раскладка плитки. Прихожая. Коридор. Санузел. Ванная


ПРЕДВАРИТЕЛЬНО · не для производства работ · открыто пунктов: 4 (реестр — л. 5)

Раскладка от чистовых размеров · размеры в мм · высоты фартука от чистого пола


Фрагмент 1. Прихожая (пом. 4). Пол 600×1200, шов 2 мм, М 1:40

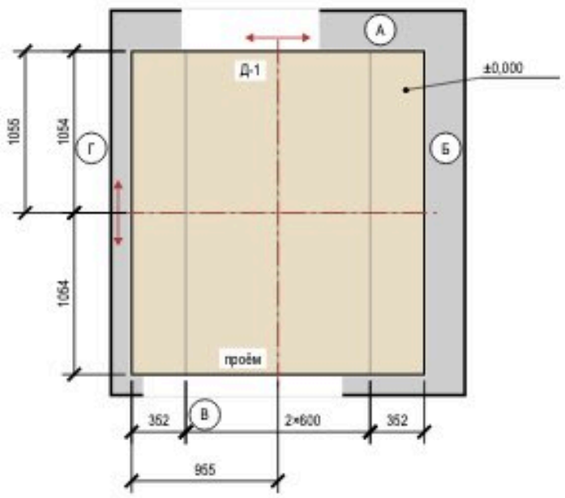


Фрагмент 2. Коридор (пом. 5). Пол 600×1200, шов 2 мм, М 1:40

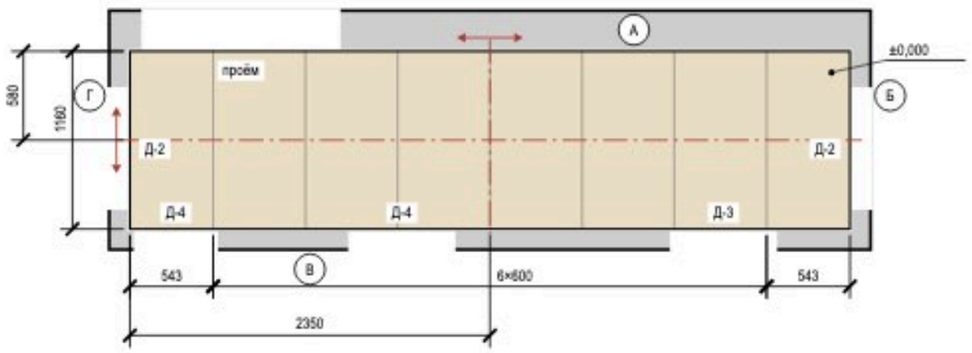

Фрагмент 3. Санузел (пом. 6). Пол 600×1200, шов 2 мм, М 1:40

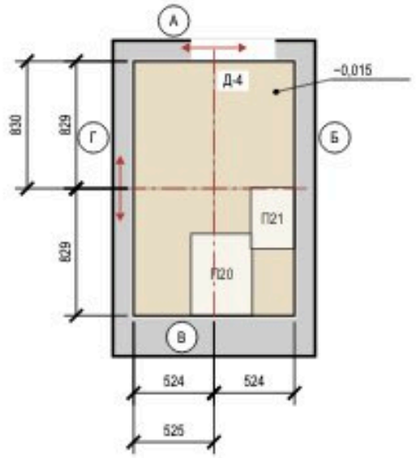

Фрагмент 4. Ванная (пом. 7). Пол 600×1200, шов 2 мм, М 1:40

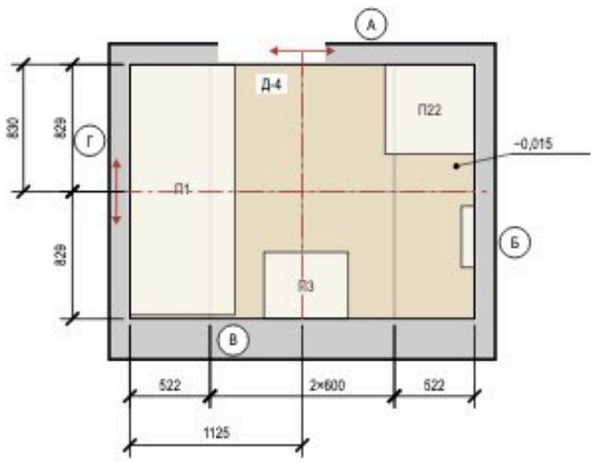

Условные обозначения

- плитка целая; тонкая линия — шов
- плитка с подрезкой (размер — на цепочке)
- ось старта; стрелки — направление укладки
- отметка чистого пола на полке выноски, м
- (А) обозначение стены А–Г (как на развёртках)

Подсчёт плитки

Поверхность	Формат	S, м²	Целых	Подр.	С запасом
Прихожая, пол	600×1200	4,15	0	8	9
Коридор, пол	600×1200	5,51	0	8	9
Санузел, пол	600×1200	1,83	0	4	5
Ванная, пол	600×1200	3,85	0	8	9

Примечания

1. Прихожая: керамогранит 600×1200, длинная сторона — вдоль стен Б и Г, шов 2 мм, прямая раскладка от центра. Стены окрашены: раскладка от чистового контура минус штукатурка и шпаклёвка 15 мм на сторону (принято); подрезки 352 / 1054 мм, срез — под плинтус.
2. Прихожая: деформационный зазор по периметру 8–10 мм под плинтусом; в проёмах — стык с соседним покрытием по оси полотна двери. Клей С2, затирка класс не задан.
3. Коридор: керамогранит 600×1200, длинная сторона — вдоль стен Б и Г, шов 2 мм, прямая раскладка от центра. Стены окрашены: раскладка от чистового контура минус штукатурка и шпаклёвка 15 мм на сторону (принято); подрезки 543 / 1160 мм, срез — под плинтус.
4. Коридор: деформационный зазор по периметру 8–10 мм под плинтусом; в проёмах — стык с соседним покрытием по оси полотна двери. Клей С2, затирка класс не задан.
5. Санузел: керамогранит 600×1200, длинная сторона — вдоль стен Б и Г, шов 2 мм, прямая раскладка от центра. Стены окрашены: раскладка от чистового контура минус штукатурка и шпаклёвка 15 мм на сторону (принято); подрезки 524 / 829 мм, срез — под плинтус.
6. Санузел: деформационный зазор по периметру 8–10 мм под плинтусом; в проёмах — стык с соседним покрытием по оси полотна двери. Клей С2 S1, затирка класс не задан.
7. Ванная: керамогранит 600×1200, длинная сторона — вдоль стен Б и Г, шов 2 мм, прямая раскладка от центра. Стены окрашены: раскладка от чистового контура минус штукатурка и шпаклёвка 15 мм на сторону (принято); подрезки 522 / 829 мм, срез — под плинтус.
8. Ванная: деформационный зазор по периметру 8–10 мм под плинтусом; в проёмах — стык с соседним покрытием по оси полотна двери. Клей С2 S1, затирка класс не задан.
9. Клей, затирка и итог по форматам — в ведомостях листа «Раскладка плитки. Планы полов».

Допущения и предложения на листе

Основа листа: размеры сняты с растрового плана заказчика без размеров: масштаб восстановлен по площадям помещений (≈ 11,8 мм на пиксель), контрольный обмер не выполнен (К-1); высота потолка 2700 мм принята: на плане заказчика её нет (К-2); толщины стен 300 / 120 мм приняты по плану заказчика, не замерены (К-1); разрешённая мощность 15 кВт принята по типовым ТУ для квартиры, ТУ заказчиком не переданы (К-4).

См. лист открытых вопросов (лист 5, записи К-1, К-2, К-4).

1000 мм · печать 1:1

Изм.	Кол.уч	Лист	№ док.	Подп.	Дата
Разраб.		Кырпан А.С.			09.10.26
Пров.					
ГИП					
Н. контр.					
Утв.					

ГД-2026-007-АИ

Квартира 65 м²

Общая площадь 65,24* м² · * размеры со скана, не замерены (реестр — л. 5, К-1)

Дизайн-проект интерьера

Стадия	Лист	Листов
РП	33	79

Раскладка плитки. Прихожая. Коридор. Санузел. Ванная

М 1:40

Кырпан Александр Сергеевич

выпуск 09.10.2026 № 147dabfd23 · стр. 41 из 110

07

Полы и отделка

Кырлан Александр Сергеевич

выпуск 09.10.2026 № 147dabfd23 · стр. 42 из 110


План полов

Покрытия, направление укладки, отметки чистого пола, стыки · размеры в мм · отметки в м

ПРЕДВАРИТЕЛЬНО · не для производства работ · открыто пунктов: 4 (реестр — л. 5)

Экспликация полов

Номер помещения	Тип пола	Схема пола	Данные элементов пола (наименование, толщина, основание), мм	Площадь, м²
1, 9	1		Инженерная доска на клею — 14 Стяжка ЦПС М200 — 50 Плита перекрытия Всего 64 мм; ЧП ±0,000, верх плиты −0,064	20,22
2, 3, 8	2		Инженерная доска, IM1848, 1380×190 мм, на клею ЧП ±0,000	29,68
4, 5	3		Керамогранит, SG501600R, 600×1200 мм ЧП ±0,000	9,66
6, 7	4		Керамогранит, SG501600R, 600×1200 мм Гидроизоляция обмазочная, 2 слоя, с заведением на стены 200 мм ЧП −0,015	5,68
			Итого	**65,24**

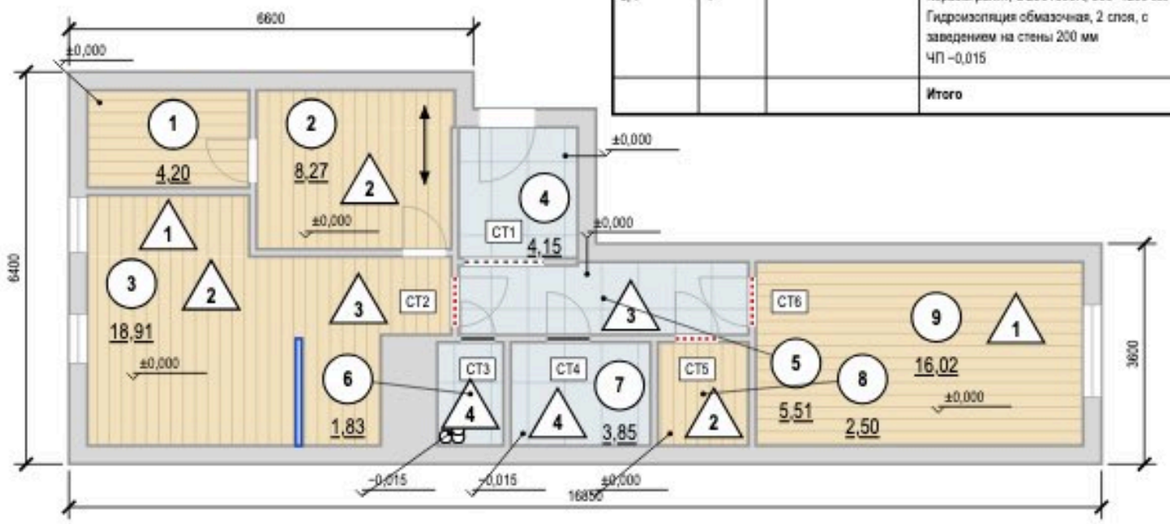

Стыки покрытий в проёмах

Марка	Проём	Типы пола	Отметки ЧП	Решение
CT1	4–5	3 / 3	±0,000 / ±0,000	б/п
CT2	5–3 (Д-2)	3 / 2	±0,000 / ±0,000	не задано
CT3	5–6 (Д-4)	3 / 4	±0,000 / −0,015	порог h=15 мм
CT4	5–7 (Д-4)	3 / 4	±0,000 / −0,015	порог h=15 мм
CT5	5–8 (Д-3)	3 / 2	±0,000 / ±0,000	не задано
CT6	5–9 (Д-2)	3 / 1	±0,000 / ±0,000	не задано

Условные обозначения

- тип 1 — инженерная доска, линии — вдоль доски
- тип 2 — инженерная доска, линии — вдоль доски
- тип 3 — керамогранит 600×1200, сетка — формат плитки
- тип 4 — керамогранит 600×1200, сетка — формат плитки
- 1 — номер типа пола (экспликация полов)
- схема пола, без масштаба: плита — штриховка, стяжка точки, звукоизоляция — зигзаг, гидроизоляция — утолщённая линия с заведением на стену
- направление укладки (длинная сторона доски)
- ±0,000 — отметка чистого пола, м
- стык в проёме: без порога (б/п)
- стык в проёме: решение не задано
- стык в проёме: порог
- CT1 — марка стыка (ведомость стыков)
- стояк К1 — канализация, В1 — ХВС, Т3 — ГВС
- новое — возводится по проекту (синим)
- 1 — номер помещения, площадь м²

Отметки по высоте

±0,000	чистый пол пом. 1–5, 8, 9; отсчёт высот
−0,015	чистый пол пом. 6, 7, ниже на 15 мм
−0,064*	верх плиты — расчёт, не замер (задание на обмер)
сущ. пол	снимается до плиты; не замерен (задание на обмер)

Примечания

1. За отметку ±0,000 принят чистый пол, не существующий (блок отметок). Площади — по чистым размерам помещений, м²; размеры — в мм.
2. Стык разнотипных покрытий — по оси дверного полотна (под полотном в закрытом положении); решение стыка — по ведомости стыков.
3. Пол санузлов ниже смежных помещений на 15 мм за счёт меньшей толщины стяжки (верх плиты общий — по экспликации полов); гидроизоляция по стяжке с заведением на стены не менее 200 мм (СП 29.13330.2011, п. 7.2), до облицовки — тест проливом и акт скрытых работ.
4. Выпуски канализации с уклоном и трассы водоснабжения — в слое засыпки под стяжкой (по экспликации полов); отметки, уклоны и прочистки — по листу разводки ВК.28.
5. Звукоизоляционный слой под стяжкой проектом не предусмотрен (стяжка по плите): приведённый уровень ударного шума перекрытия с полом Lnw не более 60 дБ (СП 51.13330.2011, табл. 2) подтвердить по данным дома; при превышении — плавающая стяжка по звукоизоляции с демпферной лентой по контуру и у стояков, пирог пересчитать.
6. Штучные покрытия (инженерная доска): направление — по стрелке; влажность основания по СМ не более 2,0 % (по ТУ изготовителя).
7. Ровность основания — просвет под 2-метровой рейкой не более 2 мм: пом. 1, 2, 3, 8, 9 (инженерная доска), пом. 4, 5, 6, 7 (керамогранит); проверить до укладки покрытия (СП 71.13330.2017, табл. 8.5).
8. Сетка на плитке — условная, в размер формата; точка старта и раскладка — по листу раскладки плитки.
9. Пироги полов — по экспликации полов: слои сверху вниз, толщины в мм; гидроизоляция мокрых зон — в пироге и в ведомости отделки; схема пола — без масштаба.

1000 мм · печать 1:1

Допущения и предложения на листе

Основа листа: размеры сняты с растрового плана заказчика без размеров: масштаб восстановлен по площадям помещений (≈ 11,8 мм на пиксель), контрольный обмер не выполнен (К-1); высота потолка 2700 мм принята: на плане заказчика её нет (К-2); толщины стен 300 / 120 мм приняты по плану заказчика, не замерены (К-1); разрешённая мощность 15 кВт принята по типовым ТУ для квартиры, ТУ заказчиком не переданы (К-4).

См. лист открытых вопросов (лист 5, записи К-1, К-2, К-4).

Изм.	Кол.уч	Лист	№ док.	Подп.	Дата
Разраб.		Кырпан А.С.			09.10.26
Пров.					
ГИП					
Н. контр.					
Утв.					

ГД-2026-007-АИ

Квартира 65 м²

Общая площадь 65,24* м² · * размеры со скана, не замерены (реестр — п. 5, К-1)

Дизайн-проект интерьера

Стадия	Лист	Листов
РП	34	79

План полов

М 1:100

Кырпан Александр Сергеевич

выпуск 09.10.2026 · 147dabfd23 · стр. 43 из 110

Ведомость отделки помещений

Потолки, стены, низ стен, полы · площади в м², длины в м · отметки в м

Ведомость отделки помещений (форма 1 прил. А ГОСТ 21.501-2018)

№	Наименование помещения	Потолок			Стены и перегородки			Низ стен (плинтус)			Пол		Примечание
		Вид отделки	Код цвета	S, м²	Вид отделки	Код цвета	S, м²	Вид отделки	Код цвета	L, м	Вид отделки	S, м²	
1	Гардеробная 4,20 м²	Окраска, Tikkurila Anti-Reflex 2, глубокоматовая, 2 слоя, подготовка Q3	Tikkurila V503	4,20	Окраска, Tikkurila Harmony, матовая, 2 слоя, подготовка Q3	Tikkurila V503	21,37	Плинтус МДФ h=69 мм, SX165	Tikkurila V503	7,8	Инженерная доска, IM1848, 1380×190 мм, на клею; тип 1, отм. ЧП ±0,000	4,20	H стен 2700 (до потолка); плинтус в цвет: стены
2	Спальня 8,27 м²	Окраска, Tikkurila, глубокоматовая	NCS S 0300-N	8,27	Окраска, Tikkurila, глубокоматовая, подготовка Q3	NCS S 1502-Y50R	28,54	Плинтус МДФ h=69 мм, SX165	NCS S 0300-N	10,3	Инженерная доска, IM1848, 1380×190 мм, на клею; тип 2, отм. ЧП ±0,000	8,27	H стен 2700 (до потолка)
3	Кухня-гостиная 18,91 м²	Окраска, Tikkurila, глубокоматовая	NCS S 0300-N	18,91	Окраска, Tikkurila, полуматовая, подготовка Q3	NCS S 1002-Y50R	48,29	Плинтус МДФ h=69 мм, SX165	NCS S 0300-N	18,6	Инженерная доска, IM1848, 1380×190 мм, на клею; тип 2, отм. ЧП ±0,000	18,91	H стен 2700 (до потолка)
4	Прихожая 4,15 м²	Окраска, Tikkurila, глубокоматовая	NCS S 0300-N	4,15	Окраска, Tikkurila, полуматовая, подготовка Q3	NCS S 1502-Y50R	17,41	Плинтус МДФ h=69 мм, SX165	NCS S 0300-N	6,0	Керамогранит, SG501600R, 600×1200 мм; тип 3, отм. ЧП ±0,000	4,15	H стен 2700 (до потолка)
5	Коридор 5,51 м²	Окраска, Tikkurila, глубокоматовая	NCS S 0300-N	5,51	Окраска, Tikkurila, полуматовая, подготовка Q3	NCS S 1502-Y50R	21,78	Плинтус МДФ h=69 мм, SX165	NCS S 0300-N	7,0	Керамогранит, SG501600R, 600×1200 мм; тип 3, отм. ЧП ±0,000	5,51	H стен 2700 (до потолка)
6	Санузел 1,83 м²	Окраска, Tikkurila, глубокоматовая	NCS S 0300-N	1,83	Облицовка плиткой, 610010001195, 600×1200 мм, клей C2	Italon 610010001195	13,89	нет (облицовка от пола)			Керамогранит, SG501600R, 600×1200 мм; тип 4, отм. ЧП −0,015	1,83	H стен 2715 (до потолка); гидроизоляция обмазочная, 2 слоя, с заведением на стены 200 мм (по пирогу пола); тест проливом и акт скрытых работ
7	Ванная 3,85 м²	Окраска, Tikkurila, глубокоматовая	NCS S 0300-N	3,85	Облицовка плиткой, 610010001195, 600×1200 мм, клей C2	Italon 610010001195	20,09	нет (облицовка от пола)			Керамогранит, SG501600R, 600×1200 мм; тип 4, отм. ЧП −0,015	3,85	H стен 2715 (до потолка); тёплый пол; гидроизоляция обмазочная, 2 слоя, с заведением на стены 200 мм (по пирогу пола); тест проливом и акт скрытых работ
8	Кладовая 2,50 м²	Окраска, Tikkurila, глубокоматовая	NCS S 0300-N	2,50	Окраска, Tikkurila, матовая, подготовка Q3	NCS S 0502-Y	15,65	Плинтус МДФ h=69 мм, SX165	NCS S 0300-N	5,6	Инженерная доска, IM1848, 1380×190 мм, на клею; тип 2, отм. ЧП ±0,000	2,50	H стен 2700 (до потолка)
9	Детская 16,02 м²	Окраска, Tikkurila Anti-Reflex 2, глубокоматовая, 2 слоя, подготовка Q3	Tikkurila V503	16,02	Окраска, Farrow & Ball Modern Emulsion, матовая, 2 слоя, подготовка Q3 Акцент — стена А: окраска, Farrow & Ball Modern Emulsion, матовая, 2 слоя, подготовка Q3	Farrow & Ball No. 241 Farrow & Ball No. 30	26,54 14,42	Плинтус МДФ h=69 мм, SX165	Farrow & Ball No. 241	15,9	Инженерная доска, IM1848, 1380×190 мм, на клею; тип 1, отм. ЧП ±0,000	16,02	H стен 2700 (до потолка); плинтус в цвет: стены
	Итого			**65,24**			**227,98**			**71,1**		**65,24**	

Допущения и предложения на листе

Основа листа: размеры сняты с растрового плана заказчика без размеров: масштаб восстановлен по площадям помещений (≈ 11,8 мм на пиксель), контрольный обмер не выполнен (К-1); высота потолка 2700 мм принята: на плане заказчика её нет (К-2); толщины стен 300 / 120 мм приняты по плану заказчика, не замерены (К-1); разрешённая мощность 15 кВт принята по типовым ТУ для квартиры, ТУ заказчиком не переданы (К-4).

См. лист открытых вопросов (лист 5, записи К-1, К-2, К-4).

Примечания

1. Площади поверхностей — по чистым граням стен до отделки: стены = периметр × высоту от чистого пола помещения до низа потолка минус проёмы (облицовка плиткой — до верха облицовки); плинтус = периметр минус дверные проёмы; пол и потолок — по площади помещения. Количество плиток по раскладке. Площади помещений — с учётом всех частей помещения; откосы в площадь стен не входят.
2. Акцентные стены — отдельными строками, их площадь вычтена из основной отделки стен помещения.
3. Плинтус — длина по периметру за вычетом дверных проёмов; примыкания к наличникам и встроенной мебели — по развёрткам.
4. Формат плитки — Ш×В×Т (ширина × высота в положении укладки × толщина), мм; на полу — вдоль стен А/В × вдоль стен Б/Г.
5. Коды цвета — по веерам производителей; колеровка каждой краски одной партией, проверка выкраса при свете D65 и при лампах проекта.
6. Уровни подготовки Q1–Q4 — система Knauf, не норма ГОСТ/СП; допуски поверхностей — по СП 71.13330.2017 (действующая редакция).
7. «аналог:» — изделие задано характеристиками, марку и артикул согласовать с заказчиком до закупки.
8. Сводка площадей по материалам, м²: потолок — Tikkurila V503 Anti-Reflex 2 — 20,22; потолок — NCS S 0300-N — 45,02; стены — Tikkurila V503 Harmony — 21,37; стены — NCS S 1502-Y50R — 67,74; стены — NCS S 1002-Y50R — 48,29; стены — облицовка плиткой 600×1200 мм, Italon 610010001195 — 33,97; стены — NCS S 0502-Y — 15,65; стены — Farrow & Ball No. 241 Modern Emulsion — 26,54; стены — Farrow & Ball No. 30 Modern Emulsion 14,42.

Изм.	Кол.уч	Лист	№ док.	Подп.	Дата	ГД-2026-007-АИ			
Разраб.		Кырпан А.С.			09.10.26	Квартира 65 м²			
Пров.						Общая площадь 65,24* м² · * размеры со скана, не замерены (реестр — п. 5, К-1)			
ГИП						Дизайн-проект интерьера	Стадия	Лист	Листов
							РП	35	79
Н. контр.						Ведомость отделки помещений	Кырпан Александр Сергеевич		
Утв.						М 6/м			

выпуск 09.10.2026 № 147dabfd23 · стр. 44 из 110

Колерная карта

Цвета и материалы по помещениям · палитра проекта · выкрасы на согласование

Колерная карта по помещениям


Помещение	Поверхность	Образец	Поз.	Система и код цвета	Производитель, линейка / материал, артикул	Блеск	Класс EN 13300	LRV	Площадь
1. Гардеробная 4,2 м²	стены		K1	Tikkurila V503	Tikkurila · Harmony	матовая	1	86	21,4 м²
	потолок		K2	Tikkurila V503	Tikkurila · Anti-Reflex 2	глубокомат.	2	86	4,2 м²
	пол		KM1	по образцу	Quick-Step · Impressive				4,2 м²
	плинтус		K3	Tikkurila V503	Orac Decor · Contour (Luxxus)			86	7,8 м
2. Спальня 8,27 м²	стены		K4	NCS S 1502-Y50R	Tikkurila	глубокомат.	2	72	28,5 м²
	потолок		K5	NCS S 0300-N	Tikkurila	глубокомат.	2	92	8,3 м²
	пол		KM1	по образцу	Quick-Step · Impressive				8,3 м²
	плинтус		K6	NCS S 0300-N	Orac Decor · Contour (Luxxus)	полуматов.		92	10,3 м
3. Кухня-гостиная 18,91 м²	стены		K7	NCS S 1002-Y50R	Tikkurila	полуматов.	1	82	48,3 м²
	потолок		K8	NCS S 0300-N	Tikkurila	глубокомат.	1	92	18,9 м²
	пол		KM1	по образцу	Quick-Step · Impressive				18,9 м²
	плинтус		K6	NCS S 0300-N	Orac Decor · Contour (Luxxus)	полуматов.		92	18,6 м
4. Прихожая 4,15 м²	стены		K9	NCS S 1502-Y50R	Tikkurila	полуматов.	1	72	17,4 м²
	потолок		K8	NCS S 0300-N	Tikkurila	глубокомат.	1	92	4,2 м²
	пол		K10	Kerama Marazzi SG501600R	Kerama Marazzi · Королевская дорога				4,2 м²
	плинтус		K6	NCS S 0300-N	Orac Decor · Contour (Luxxus)	полуматов.		92	6,0 м
5. Коридор 5,51 м²	стены		K9	NCS S 1502-Y50R	Tikkurila	полуматов.	1	72	21,8 м²
	потолок		K8	NCS S 0300-N	Tikkurila	глубокомат.	1	92	5,5 м²
	пол		K10	Kerama Marazzi SG501600R	Kerama Marazzi · Королевская дорога				5,5 м²
	плинтус		K6	NCS S 0300-N	Orac Decor · Contour (Luxxus)	полуматов.		92	7,0 м
6. Санузел 1,83 м²	стены		K11	Italon 610010001195	Italon · Charme Extra				13,9 м²
	потолок		K8	NCS S 0300-N	Tikkurila	глубокомат.	1	92	1,8 м²
	пол		K10	Kerama Marazzi SG501600R	Kerama Marazzi · Королевская дорога				1,8 м²
7. Ванная 3,85 м²	стены		K11	Italon 610010001195	Italon · Charme Extra				20,1 м²
	потолок		K8	NCS S 0300-N	Tikkurila	глубокомат.	1	92	3,9 м²
	пол		K10	Kerama Marazzi SG501600R	Kerama Marazzi · Королевская дорога				3,9 м²
8. Кладовая 2,5 м²	стены		K12	NCS S 0502-Y	Tikkurila	матовая	2	86	15,6 м²
	потолок		K5	NCS S 0300-N	Tikkurila	глубокомат.	2	92	2,5 м²
	пол		KM1	по образцу	Quick-Step · Impressive				2,5 м²
	плинтус		K6	NCS S 0300-N	Orac Decor · Contour (Luxxus)	полуматов.		92	5,6 м
9. Детская 16,02 м²	стены		K13	Farrow & Ball No. 241	Farrow & Ball · Modern Emulsion	матовая	1	67	26,5 м²
	акцент А		K14	Farrow & Ball No. 30	Farrow & Ball · Modern Emulsion	матовая	1	7	14,4 м²
	потолок		K2	Tikkurila V503	Tikkurila · Anti-Reflex 2	глубокомат.	2	86	16,0 м²
	пол		KM1	по образцу	Quick-Step · Impressive				16,0 м²
	плинтус		K15	Farrow & Ball No. 241	Orac Decor · Contour (Luxxus)			67	15,9 м

Схема палитры проекта


Стиль: Скандинавский · схема: нейтральная

основной	второстепенный	второстепенный	акцентный
NCS S 0500-N	**NCS S 1500-N**	**NCS S 2002-Y**	**NCS S 4010-R90B**
нейтральный белый LRV 85 в отделке не применён	светлый нейтральный серый LRV 64 в отделке не применён	серый камень, тёплый LRV 55 в отделке не применён	пыльный синий LRV 27 в отделке не применён

План 60/30/10

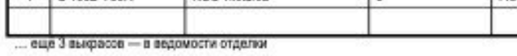

Окраска, факт — по площади стен, акцентов, потолков

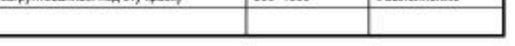

окрашено всего 293,2 м²; второстепенный тон несут мебель и текстиль

Текстиль и декор в цветах вне палитры проекта

- Tikkurila H487 Pumice — пом. 9 (T7)
- Tikkurila V503 Winter — пом. 9 (T8)
- Tikkurila V484 Driftwood — пом. 9 (T9)
- Farrow & Ball No. 229 Elephant's Breath — пом. 9 (T10)
- Farrow & Ball No. 47 Green Smoke — пом. 9 (T11)
- Farrow & Ball No. 30 Hague Blue — пом. 9 (T12)

Условные обозначения

- K1 Tikkurila V503 · Winter · Harmony · матовая · кл. 1
- K2 Tikkurila V503 · Winter · Anti-Reflex 2 · глубокомат. · кл. 2
- K3 Tikkurila V503 · Winter · Contour (Luxxus)
- K4 NCS S 1502-Y50R · Tikkurila · глубокомат. · кл. 2
- K5 NCS S 0300-N · Tikkurila · глубокомат. · кл. 2
- K6 NCS S 0300-N · Orac Decor Contour (Luxxus) · полуматов.
- K7 NCS S 1002-Y50R · Tikkurila · полуматов. · кл. 1
- K8 NCS S 0300-N · Tikkurila · глубокомат. · кл. 1
- K9 NCS S 1502-Y50R · Tikkurila · полуматов. · кл. 1
- K10 Kerama Marazzi SG501600R · Королевская дорога · Королевская дорога
- K11 Italon 610010001195 · Charme Extra · Charme Extra
- K12 NCS S 0502-Y · Tikkurila · матовая · кл. 2
- K13 Farrow & Ball No. 241 · Skimming Stone · Modern Emulsion · матовая · кл. 1
- K14 Farrow & Ball No. 30 · Hague Blue · Modern Emulsion · матовая · кл. 1
- K15 Farrow & Ball No. 241 · Skimming Stone · Contour (Luxxus)
- KM1 инженерная доска · IM1848

дерево (доска, паркет, ламинат) — рисунок досок

HEX не задан — цвет только по коду и вееру

К — позиция окраски (код + продукт + блеск), КМ — позиция материала, тон КМ — по описанию артикула, эталон — образец материала; ≈ LRV — расчёт по HEX, справочно

Перечень выкрасов на согласование

№	Код	Бренд / веер	Пом. / стена	Подложка	Формат	Статус
1	V503	Tikkurila	1, 9	ГКЛ, загрунтованный под эту краску; МДФ, загрунтованный под эмаль	600×1000; 300×600	к выполнению
2	S 1502-Y50R	NCS Tikkurila	2, 4, 5	ГКЛ, загрунтованный под эту краску	600×1000	к выполнению
3	S 0300-N	NCS Tikkurila	2, 3, 4, 5, 6, 7, 8	ГКЛ, загрунтованный под эту краску; МДФ, загрунтованный под эмаль	600×1000; 300×600	к выполнению
4	S 1002-Y50R	NCS Tikkurila	3	ГКЛ, загрунтованный под эту краску	600×1000	к выполнению

… ещё 3 выкрасов — в ведомости отделки

Примечания

1. Цвет утверждается только по выкрасу на объекте: формат от А3 до 1000×1000 мм на загрунтованном ГКЛ, в 2 слоя (как на стене), не на белой шпаклёвке; смотреть днём и при свете проекта своего помещения, рядом с образцами пола и фасадов. Подпись на обороте: код, бренд и веер, дата.
2. Колеровка машинная в колеровочном центре бренда; каждый код — за один проход, одной партией на весь объём. Колеровщику передаётся только система и код утверждённого веера; плашки и HEX на листе — ориентир, печать не является эталоном цвета.
3. Класс мокрого истирания — EN 13300 (ISO 11998); блеск — по ГОСТ 31975 (ISO 2813), геометрия 60°. LRV — пересчёт координаты L* каталога производителя (Y = ((L*+16)/116)³); «≈» — расчёт по HEX, справочно.
4. Площади поверхностей — тем же способом и с теми же цифрами, что в ведомости отделки (способ счёта — в общих указаниях); объём краски к заказу, фасовка и материалы КМ — в спецификации отделочных материалов.
5. Перечень выкрасов составлен по кодам колерной карты; к основному тону стен добавить на выкрас 2 соседних тона того же веера (светлее и темнее), статус отмечать в графе «Статус» при согласовании.

Допущения и предложения на листе. Основа листа: размеры сняты с растрового плана заказчика без размеров: масштаб восстановлен по площадям помещений (≈ 11,8 мм на пиксель), контрольный обмер не выполнен (К-1); высота потолка 2700 мм принята: на плане заказчика её нет (К-2); толщины стен 300 / 120 мм приняты по плану заказчика, не замерены (К-1); разрешённая мощность 15 кВт принята по типовым ТУ для квартиры, ТУ заказчиком не переданы (К-4). См. лист открытых вопросов (лист 5, записи К-1, К-2, К-4).

Изм.	Кол.уч	Лист	№ док.	Подп.	Дата
Разраб.		Кырпан А.С.			09.10.26
Пров.					
ГИП					
Н. контр.					
Утв.					

ГД-2026-007-АИ

Квартира 65 м²

Общая площадь 65,24* м² · * размеры со скана, не замерены (реестр — л. 5, К-1)

Дизайн-проект интерьера

Стадия	Лист	Листов
РП	36	79

Колерная карта

М 6/м

Кырпан Александр Сергеевич

выпуск 09.10.2026 · 147dabfd23 · стр. 45 из 110

Спецификация отделочных материалов

ПРЕДВАРИТЕЛЬНО · не для производства работ · открыто пунктов: 4 (реестр — л. 5)

Форма 1 по ГОСТ 21.110-2013 · количества — из геометрии проекта, с запасом · часть 1 из 2

Поз.	Наименование и техническая характеристика	Тип, марка, обозначение документа	Код продукции	Поставщик	Ед. изм.	Кол.	Масса 1 ед., кг	Примечание
	Лакокрасочные материалы							
1	Краска интерьерная водно-дисперсионная акриловая для стен, матовая, класс мокрого истирания 1 по EN 13300, база A; цвет Tikkurila V503 «Winter», колеровка машинная	Tikkurila Harmony		Tikkurila	л	6,3		поз. К1 колерной карты; пом. 1; S = 21,4 м² × 2 сл. × 0,12 л/м² = 5,1 л, +10 % и 0,5 л на подкраску → ≥ 6,1 л; тара 2 × 2,7 л + 1 × 0,9 л
2	Краска интерьерная водно-дисперсионная акриловая для потолков, глубокоматовая, класс мокрого истирания 2 по EN 13300, база A; цвет Tikkurila V503 «Winter», колеровка машинная	Tikkurila Anti-Reflex 2		Tikkurila	л	6,3		поз. К2 колерной карты; пом. 1, 9; S = 20,2 м² × 2 сл. × 0,12 л/м² = 4,9 л, +10 % и 0,5 л на подкраску → ≥ 5,6 л; тара 2 × 2,7 л + 1 × 0,9 л
3	Краска интерьерная водно-дисперсионная акриловая для стен, глубокоматовая, класс мокрого истирания 2 по EN 13300, база A; цвет NCS S 1502-Y50R, колеровка машинная	Tikkurila		Tikkurila	л	8,1		поз. К4 колерной карты; пом. 2; S = 28,5 м² × 2 сл. × 0,12 л/м² = 6,9 л, +10 % и 0,5 л на подкраску → ≥ 8,0 л; тара 3 × 2,7 л
4	Краска интерьерная водно-дисперсионная для потолков, глубокоматовая, класс мокрого истирания 2 по EN 13300, база A; цвет NCS S 0300-N, колеровка машинная	Tikkurila		Tikkurila	л	3,6		поз. К5 колерной карты; пом. 2, 8; S = 10,8 м² × 2 сл. × 0,12 л/м² = 2,6 л, +10 % и 0,5 л на подкраску → ≥ 3,3 л; тара 1 × 2,7 л + 1 × 0,9 л
5	Краска интерьерная водно-дисперсионная акриловая для стен, полуматовая, класс мокрого истирания 1 по EN 13300, база A; цвет NCS S 1002-Y50R, колеровка машинная	Tikkurila		Tikkurila	л	13,5		поз. К7 колерной карты; пом. 3; S = 48,3 м² × 2 сл. × 0,12 л/м² = 11,6 л, +10 % и 0,5 л на подкраску → ≥ 13,2 л; тара 1 × 9 л + 1 × 2,7 л + 2 × 0,9 л
6	Краска интерьерная водно-дисперсионная для потолков, глубокоматовая, класс мокрого истирания 1 по EN 13300, база A; цвет NCS S 0300-N, колеровка машинная	Tikkurila		Tikkurila	л	9,9		поз. К8 колерной карты; пом. 3, 4, 5, 6, 7; S = 34,3 м² × 2 сл. × 0,12 л/м² = 8,2 л, +10 % и 0,5 л на подкраску → ≥ 9,5 л; тара 1 × 9 л + 1 × 0,9 л
7	Краска интерьерная водно-дисперсионная акриловая для стен, полуматовая, класс мокрого истирания 1 по EN 13300, база A; цвет NCS S 1502-Y50R, колеровка машинная	Tikkurila		Tikkurila	л	11,7		поз. К9 колерной карты; пом. 4, 5; S = 39,2 м² × 2 сл. × 0,12 л/м² = 9,4 л, +10 % и 0,5 л на подкраску → ≥ 10,8 л; тара 1 × 9 л + 1 × 2,7 л
8	Краска интерьерная водно-дисперсионная акриловая для стен, матовая, класс мокрого истирания 2 по EN 13300, база A; цвет NCS S 0502-Y, колеровка машинная	Tikkurila		Tikkurila	л	5,4		поз. К12 колерной карты; пом. 8; S = 15,6 м² × 2 сл. × 0,12 л/м² = 3,8 л, +10 % и 0,5 л на подкраску → ≥ 4,6 л; тара 2 × 2,7 л
9	Краска интерьерная водно-дисперсионная акриловая для стен, матовая, класс мокрого истирания 1 по EN 13300, база A; цвет Farrow & Ball No. 241 «Skimming Stone», колеровка машинная	Farrow & Ball Modern Emulsion		Farrow & Ball	л	10		поз. К13 колерной карты; пом. 9; S = 26,5 м² × 2 сл. × 0,12 л/м² = 6,4 л, +10 % и 0,5 л на подкраску → ≥ 7,5 л; тара 2 × 5 л
10	Краска интерьерная водно-дисперсионная акриловая для акцентных стен, матовая, класс мокрого истирания 1 по EN 13300, база C; цвет Farrow & Ball No. 30 «Hague Blue», колеровка машинная	Farrow & Ball Modern Emulsion		Farrow & Ball	л	5		поз. К14 колерной карты; пом. 9; S = 14,4 м² × 2 сл. × 0,12 л/м² = 3,5 л, +10 % и 0,5 л на подкраску → ≥ 4,3 л; тара 1 × 5 л
11	Краска для МДФ и дерева в цвет Tikkurila V503 «Winter» — окраска плинтуса; блеск не ниже блеска стен	марка не задана			л	0,5		поз. К3; пом. 1; L = 7,8 м, S = 0,7 м² × 2 сл. × 0,12 л/м² + 10 %; продукт подобрать в веере Tikkurila
12	Акрил, полуматовая в цвет NCS S 0300-N — окраска плинтуса	аналог по характеристикам			л	1,1		поз. К6; пом. 2, 3, 4, 5, 8; L = 47,4 м, S = 4,0 м² × 2 сл. × 0,12 л/м² + 10 %; продукт подобрать в веере NCS
13	Краска для МДФ и дерева в цвет Farrow & Ball No. 241 «Skimming Stone» — окраска плинтуса; блеск не ниже блеска стен	марка не задана			л	0,5		поз. К15; пом. 9; L = 15,9 м, S = 1,3 м² × 2 сл. × 0,12 л/м² + 10 %; продукт подобрать в веере Farrow & Ball

Допущения и предложения на листе

Основа листа: размеры сняты с растрового плана заказчика без размеров: масштаб восстановлен по площадям помещений (≈ 11,8 мм на пиксель), контрольный обмер не выполнен (К-1); высота потолка 2700 мм принята: на плане заказчика её нет (К-2); толщины стен 300 / 120 мм приняты по плану заказчика, не замерены (К-1); разрешённая мощность 15 кВт принята по типовым ТУ для квартиры, ТУ заказчиком не переданы (К-4).

См. лист открытых вопросов (лист 5, записи К-1, К-2, К-4).

Изм.	Кол.уч	Лист	№ док.	Подп.	Дата
Разраб.		Кырлан А.С.			09.10.26
Пров.					
ГИП					
Н. контр.					
Утв.					

ГД-2026-007-АИ

Квартира 65 м²

Общая площадь 65,24* м² · * размеры со скана, не замерены (реестр — п. 5, К-1)

Дизайн-проект интерьера	Стадия	Лист	Листов
	РП	37	79
Спецификация отделочных материалов М 6/м	**Кырлан Александр Сергеевич**		

выпуск 09.10.2026 · 147dabfd23 · стр. 46 из 110

Спецификация отделочных материалов

ПРЕДВАРИТЕЛЬНО · не для производства работ · открыто пунктов: 4 (реестр — л. 5)

Форма 1 по ГОСТ 21.110-2013 · количества — из геометрии проекта, с запасом · часть 2 из 2

Поз.	Наименование и техническая характеристика	Тип, марка, обозначение документа	Код продукции	Поставщик	Ед. изм.	Кол.	Масса 1 ед., кг	Примечание
	Лакокрасочные материалы (продолжение)							
14	Грунтовка акриловая под окраску стен и потолков — из системы производителя краски	по системе краски			м²	260		площадь окраски стен, акцентов и потолков; 1 слой перед окраской; расход — по ТУ грунтовки
	Плитка и керамогранит							
15	SG501600R, 600×1200 мм, противоскольжение R10	SG501600R		Kerama Marazzi	м²	23,04		шов 2 мм; Прихожая, пол; Коридор, пол; Санузел, пол; Ванная, пол; по раскладке 28 шт (S = 15,34 м²), с запасом 32 шт
16	610010001195, 600×1200 мм	610010001195		Italon	м²	15,28		6. Санузел, стены; раскладка не выполнена — S = 13,89 м² + 10 %; клей и затирка — по раскладке
17	610010001195, 600×1200 мм	610010001195		Italon	м²	22,10		7. Ванная, стены; раскладка не выполнена — S = 20,09 м² + 10 %; клей и затирка — по раскладке
	Напольные покрытия							
18	IM1848, рабочий слой 4 мм, эмиссия E1, укладка на клей	IM1848		Quick-Step	м²	21,7		пом. 1, 9; S = 20,22 м² + 7 % (прямая укладка); к заказу — кратно упаковке
19	IM1848, класс 33, рабочий слой 4 мм, эмиссия E1, укладка на клей	IM1848		Quick-Step	м²	31,8		пом. 2, 3, 8; S = 29,68 м² + 7 % (прямая укладка); к заказу — кратно упаковке
20	Клей для паркета и инженерной доски, эластичный (СМП / полиуретановый)	по рекомендации производителя доски			м²	50		площадь приклейки; расход и шпатель — по ТУ клея
	Погонажные изделия							
21	SX165, h = 69 мм, крепление к стене, окраска в цвет Tikkurila V503	SX165		Orac Decor	м	79		пом. 1, 2, 3, 4, 5, 8, 9; L = 71,1 м (периметр без дверных проёмов) + 10 % на подрезку; в штуках — по длине планки
	Смеси и материалы для облицовки							
22	Затирка для швов плитки	аналог по характеристикам			кг	1,2		по раскладке (a+b)/(a·b) × шов × t × 1,6 + 10 %
23	Клей плиточный C2 по EN 12004, слой 5 мм	аналог по характеристикам			кг	79		4 меш. по 25 кг; 1,5 кг/м² на 1 мм слоя + 10 %
24	Клей плиточный C2 S1 по EN 12004, слой 5 мм	аналог по характеристикам			кг	46		2 меш. по 25 кг; 1,5 кг/м² на 1 мм слоя + 10 %
25	Лента демпферная по периметру пола из плитки	аналог по характеристикам			м	27,2		периметр без дверных проёмов + 10 %

Примечания

1. Количества — из геометрии проекта: площади поверхностей по чистым граням стен до отделки (те же, что в ведомости отделки и колерной карте), плитка, клей и затирка — по раскладке плиточника; в графе «Кол.» — к заказу, с запасом.
2. Краска: расход 0,12 л/м² на слой в 2 слоя, если по ТУ не задан иной; запас 10 % и 0,5 л на подкраску каждого кода. Один код — одна партия, колеровка машинная в колеровочном центре бренда; в заказ — только после утверждения выкраса (колерная карта). Фасовка — по каталогу бренда на дату выпуска; к заказу — не меньше расчётного объёма.
3. «Аналог по характеристикам» — допускается изделие другого производителя с характеристиками не ниже указанных, по согласованию с автором проекта.
4. Графы «Код продукции» и «Масса 1 ед.» не заполнены: коды по классификатору продукции не присвоены, масса единицы до 25 кг (ГОСТ 21.110-2013).
5. Грунтовка и клей для доски указаны площадью обработки; объём — по ТУ выбранного продукта.

Допущения и предложения на листе

Основа листа: размеры сняты с растрового плана заказчика без размеров: масштаб восстановлен по площадям помещений (≈ 11,8 мм на пиксель), контрольный обмер не выполнен (К-1); высота потолка 2700 мм принята: на плане заказчика её нет (К-2); толщины стен 300 / 120 мм приняты по плану заказчика, не замерены (К-1); разрешённая мощность 15 кВт принята по типовым ТУ для квартиры, ТУ заказчиком не переданы (К-4).

См. лист открытых вопросов (лист 5, записи К-1, К-2, К-4).

Изм.	Кол.уч	Лист	№ док.	Подп.	Дата
Разраб.		Кырлан А.С.			09.10.26
Пров.					
ГИП					
Н. контр.					
Утв.					

ГД-2026-007-АИ

Квартира 65 м²

Общая площадь 65,24* м² · * размеры со скана, не замерены (реестр — л. 5, К-1)

Дизайн-проект интерьера	Стадия	Лист	Листов
	РП	38	79
Спецификация отделочных материалов М 6/м	Кырлан Александр Сергеевич		

выпуск 09.10.2026 · 147dabfd23 · стр. 47 из 110

Концепция декора и визуализации

Скандинавский · визуализации, палитра, материалы, ключевые предметы

ПРЕДВАРИТЕЛЬНО · не для производства работ · открыто пунктов: 4 (реестр — л. 5)




В1. Вид сверху (3D): планировка с мебелью, текстилем и декором


Расстановка — по плану мебели (лист 15); шторы, ковры, картины и растения — по плану текстиля и декора (лист 40).



В14. Кухня-гостиная (пом. 3)

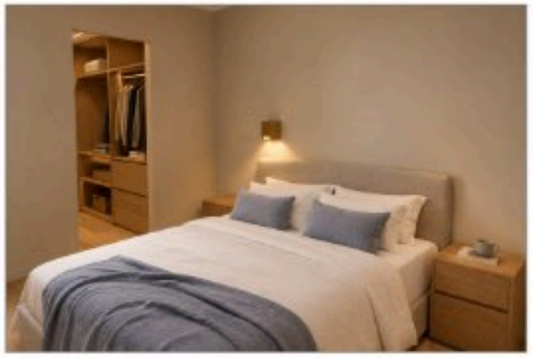


В4. Спальня (пом. 2)

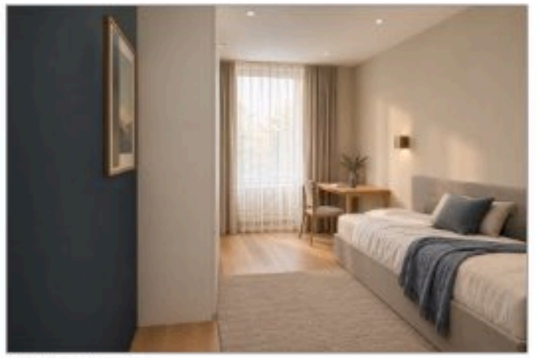

В10. Детская (пом. 9)

шторы Т7, Т8 · ковёр Т9 · картина ДК3 · зеркало ДК4 · подушки, пледы Т10, Т11, Т12

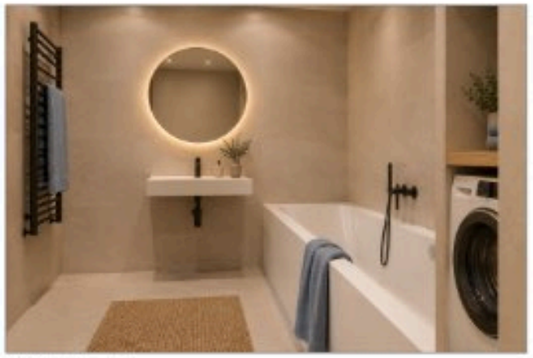

В2. Ванная (пом. 7)

Материалы и фактуры



Дуб натуральный
пол: пом. 1, 2, 3, 8, 9; рамы ДК3



Букле
подушки: Т10



Лён
портьеры: Т7



Чёрный матовый металл
рамы ДК4 — чёрный



Бархат
подушки: Т11

Ключевые предметы

— Диван М1 2200×950 — кухня-гостиная
— Кровати С1, С6
— Ковры Т9 — шерсть, на противоскользящей подложке
— Картины ДК3 — центр на высоте 1650 мм
— Зеркала в рост ДК4
— Шторы-волна Т7 (Tikkurila H487), тюль Т8 (Tikkurila V503) — в нишах потолка

Настроение

Палитра из: тёплые нейтрали NCS (стены по ведомости — S 1002-Y50R / S 1502-Y50R близки к ним), акцент — пыльный синий в текстиле. Настроение стиля: светло, спокойно, уютно (hygge), естественно, функционально, в меру (lagom). Свет тёплый, 2700–3000 K.

Примечания

1. Визуализации — образ интерьера. Изделия, размеры, высоты подвеса и привязки — по чертежам (план текстиля и декора — лист 40; шторы и карнизы — лист 41; ведомость текстиля — лист 42; ведомость декора и развеска — лист 43); при расхождении действуют чертежи и ведомости.
2. Коды цвета — ориентир подбора по веерам производителей; ткань утверждается по образцу при дневном свете и при свете проекта 2700–3000 K.
3. Мелкий стайлинг на визуализациях (книги, посуда, свечи) в ведомости не входит и поставляется заказчиком по желанию.

Палитра 60/30/10 и цвета текстиля

60 % | 30 % | 10 %

- NCS S 0500-N (нейтральный белый), LRV 85 — 60 % база
- NCS S 2002-Y (серый камень, тёплый), LRV 55 — 30 % второй цвет
- Tikkurila H487 (Pumice), LRV 57 — текстиль — Т7
- Tikkurila V484 (Driftwood), LRV 49 — текстиль — Т9
- Farrow & Ball No. 47 (Green Smoke), LRV 19 — акцент текстиля — Т11
- NCS S 1500-N (светлый нейтральный серый), LRV 64 — 30 % второй цвет
- NCS S 4010-R90B (пыльный синий), LRV 27 — 10 % акцент
- Tikkurila V503 (Winter), LRV 86 — текстиль — Т8
- Farrow & Ball No. 229 (Elephant's Breath), LRV 52 — текстиль — Т10
- Farrow & Ball No. 30 (Hague Blue), LRV 7 — акцент текстиля — Т12

Допущения и предложения на листе

Основа листа: размеры сняты с растрового плана заказчика без размеров: масштаб восстановлен по площадям помещений (≈ 11,8 мм на гипсель), контрольный обмер не выполнен (К-1); высота потолка 2700 мм принята: на плане заказчика её нет (К-2); толщины стен 300 / 120 мм приняты по плану заказчика, не замерены (К-1); разрешённая мощность 15 кВт принята по типовым ТУ для квартиры, ТУ заказчиком не переданы (К-4).
См. лист открытых вопросов (лист 5, записи К-1, К-2, К-4).


Изм.	Кол.уч	Лист	№ док.	Подп.	Дата	ГД-2026-007-АИ		
						Квартира 65 м²		
						Общая площадь 65,24* м² · * размеры со скана, не замерены (реестр — п. 5, К-1)		
Разраб.		Кырпан А.С.			09.10.26	Дизайн-проект интерьера	Стадия: РП	Лист: 39 / Листов: 79
Пров.								
ГИП								
Н. контр.						Концепция декора и визуализации	Кырпан Александр Сергеевич	
Утв.						М 6/м		

выпуск 09.10.2026 № 147dabfd23 · стр. 48 из 110

План текстиля и декора

Шторы и карнизы, ковры, картины и зеркала, растения · размеры в мм от чистовых стен и чистого пола · марки — по ведомостям

ПРЕДВАРИТЕЛЬНО · не для производства работ · открыто пунктов: 4 (реестр — л. 5)

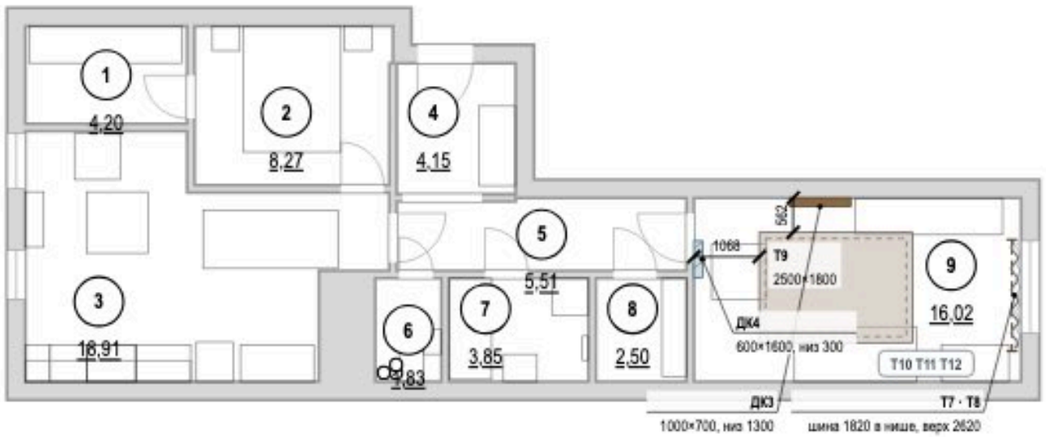

Условные обозначения

- ковёр — габарит в масштабе, цвет изделия
- шина или карниз штор (выше плоскости разреза)
- портьеры (штора-волна)
- тюль (на плане — волнистая линия)
- римская или рулонная штора в проёме
- картина на стене — ширина в масштабе
- зеркало на стене — ширина в масштабе
- растение в кашпо — диаметр в масштабе
- ваза, настольный декор
- подушки, пледы — марки на мебели
- привязка от чистовой стены, мм
- (1) номер помещения, площадь м²
- стены (подложка обмера)

Т1, ДК1 — марки по ведомостям текстиля и декора

Экспликация помещений

лист 11 · на плане — номера в марках

Окна: шина → полотно, мм

Поз.	Шина	Верх шины	Полотно, низ
Т7, Т8	1820	2620, ниша	2610, низ 10

Развеска: высоты от пола, мм

Поз.	Пом.	Ш×В	Центр	Низ	Стена
ДК3	9	1000×700	1650	1300	А
ДК4	9	600×1600	1100	300	Г

Допущения и предложения на листе

Основа листа: размеры сняты с растрового плана заказчика без размеров: масштаб восстановлен по площадям помещений (≈ 11,8 мм на пиксель), контрольный обмер не выполнен (К-1); высота потолка 2700 мм принята: на плане заказчика её нет (К-2); толщины стен 300 / 120 мм приняты по плану заказчика, не замерены (К-1); разрешённая мощность 15 кВт принята по типовым ТУ для квартиры, ТУ заказчиком не переданы (К-4).
См. лист открытых вопросов (лист 5, записи К-1, К-2, К-4).

Примечания

1. Размеры — в мм. Отступы ковров — от чистовых стен; высоты картин и зеркал — от чистого пола до центра или низа рамы.
2. Шторы — на шинах в нишах потолка (ниша — план потолков, лист 31); закладная под шину — до обшивки ГКЛ. Схемы окон, длины полотен и сборка — лист 41.
3. Картины и зеркала массой более 5 кг — на анкеры по основанию, нагрузка крепежа не меньше двойной массы изделия; на ГКЛ — только по закладной. Декор не перекрывает розетки и выключатели.
4. Ковры на гладком полу — на противоскользящей подложке.
5. Мебель — по плану расстановки мебели (лист 15); ведомость текстиля — лист 42, ведомость декора и схемы развески — лист 43.
6. Номера помещений — по экспликации (лист 11); наименования и площади на этом листе не дублируются.
7. Марки текстиля «Т» и декора «Д» относятся только к листам текстиля и декора; индексы трубопроводов Т1–Т4 — на листах ВК и ОВ.

1000 мм · печать 1:1

Изм.	Кол.уч	Лист	№ док.	Подп.	Дата
Разраб.		Кырпан А.С.			09.10.26
Пров.					
ГИП					
Н. контр.					
Утв.					

ГД-2026-007-АИ

Квартира 65 м²

Общая площадь 65,24* м² · * размеры со скана, не замерены (реестр — п. 5, К-1)

Дизайн-проект интерьера

Стадия	Лист	Листов
РП	40	79

План текстиля и декора

М 1:100

Кырпан Александр Сергеевич

выпуск 09.10.2026 № 147dabfd23 · стр. 49 из 110

08

Декор и текстиль


Кырлан Александр Сергеевич

выпуск 09.10.2026 № 147dabfd23 · стр. 50 из 110

Шторы и карнизы

Схемы окон «шина → полотно» (М 1:50) · отметки от чистого пола помещения · размеры в мм

Окно 1 — Детская (пом. 9): Т7, Т8 (М 1:50)

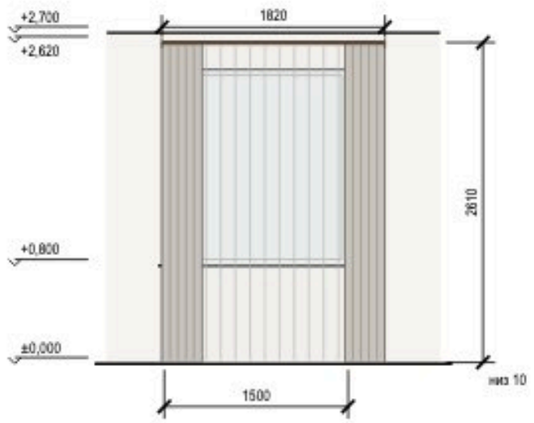

Карта окон: окно → шина → полотно

Поз.	Окно, пом.	Проём Ш×В, подоконник	Верх ниши	Изделие	Шина / карниз: длина, крепление	Верх шины	Полотно: длина, низ	Управление
Т7	1, пом. 9	1500×1600, подок. 800		портьеры	шина, 1820, в нише потолка, вынос 150	+2,620	2610, низ 10 (парит)	вручную
Т8	1, пом. 9	1500×1600, подок. 800		тюль	шина, 1820, в нише потолка, вынос 150	+2,620	2610, низ 10 (парит)	вручную

Задания смежникам

Кому	Задание	Пом.
Электрик	выводы под электрокарнизы не требуются (управление вручную)	

Условные обозначения

- портьеры в открытом положении
- римская штора: сложена / опущена
- верх ниши под шторы в потолке
- тюль (на виде окна — прозрачная плашка)
- шина или карниз на отметке верха
- оконный проём

Примечания

1. Отметки — от чистого пола помещения; размеры — мм. Длины полотен уточняются замером после чистовой отделки пола и потолка, до раскроя.
2. Карнизы — на анкеры по основанию; на ГКЛ — только по закладной.
3. Полотно портьер «парит» над полом на 10 мм; сборка портьер — 2,0, тюля — 2,5 (ширина полотна — в ведомости текстиля).
4. Электрокарнизы не предусмотрены; при замене на электропривод — вывод кабеля в нише у края шины (задание электрику).
5. Марки изделий — по плану текстиля и декора (лист 40) и ведомости текстиля (лист 42).

Допущения и предложения на листе

Основа листа: размеры сняты с растрового плана заказчика без размеров: масштаб восстановлен по площадям помещений (≈ 11,8 мм на пиксель), контрольный обмер не выполнен (К-1); высота потолка 2700 мм принята: на плане заказчика её нет (К-2); толщины стен 300 / 120 мм приняты по плану заказчика, не замерены (К-1); разрешённая мощность 15 кВт принята по типовым ТУ для квартиры, ТУ заказчиком не переданы (К-4).
См. лист открытых вопросов (лист 5, записи К-1, К-2, К-4).

Изм.	Кол.уч	Лист	№ док.	Подп.	Дата
Разраб.		Кырлан А.С.			09.10.26
Пров.					
ГИП					
Н. контр.					
Утв.					

ГД-2026-007-АИ

Квартира 65 м²

Общая площадь 65,24* м² · * размеры со скана, не замерены (реестр — п. 5, К-1)

Дизайн-проект интерьера

Стадия	Лист	Листов
РП	41	79

Шторы и карнизы

М 6/м

Кырлан Александр Сергеевич

выпуск 09.10.2026 · 147dabfd23 · стр. 51 из 110

Ведомость текстиля

Шторы, тюль, римские шторы, ковры, подушки и пледы · размеры в мм · марки — по плану текстиля и декора

Текстиль: шторы, ковры, подушки, пледы

Поз.	Пом.	Изделие	Размер, мм	Ткань, состав, плотность	Сборка, ширина полотна		Цвет (система, код)	Кол.	Примечание
T7	9	Портьеры-волна	шина 1820 × полотно 2610	лён с блэкаут-подкладкой; лён 100 %; 320 г/м²	× 2, ширина 3640		Tikkurila H487 (Pumice)	2	низ 10 (парит); в нише потолка
T8	9	Тюль	шина 1820 × полотно 2610	вуаль; полиэстер 100 %	× 2,5, ширина 4550		Tikkurila V503 (Winter)	1	низ 10 (парит); в нише потолка
T9	9	Ковёр под кроватью	2500×1800	шерсть, плоское плетение; шерсть 100 %			Tikkurila V484 (Driftwood)	1	противоскользящая подложка; ворс 8 мм
T10	9	Подушки декоративные на кровать	500×500	буклé (шерсть 60 %, полиэстер 40 %)			Farrow & Ball No. 229 (Elephant's Breath)	3	на С7
T11	9	Подушки на кровать, акцент	400×600	хлопковый бархат 100 %			Farrow & Ball No. 47 (Green Smoke)	2	на С7
T12	9	Плед на кровать	1300×1700	шерсть мериноса 100 %			Farrow & Ball No. 30 (Hague Blue)	1	на С7

образец цвета — по HEX производителя краски, справочно

Итого: шторы и тюль — 3 шт.; ковры и дорожки — 1 шт.; подушки, пледы, покрывала — 6 шт.

Образцы по помещениям

9. Детская



T7 T8 T9 T10 T11 T12

Примечания

1. Коды цвета — ориентир подбора по веерам производителей красок; ткань утверждается по образцу при дневном свете и при свете проекта 2700–3000 К.
2. Размеры полотен — по замеру после чистовой отделки пола и потолка; ширина полотна указана с учётом сборки, без припусков на швы. Схемы окон и отметки шин лист 41.
3. Портьеры и тюль — на тесьме «волна» по системе шины; блэкаут — подкладкой. Ковры — на противоскользящей подложке.
4. Замена изделия — аналогом по характеристикам (состав, плотность, размер, цвет по образцу) с согласованием автора проекта.
5. Места изделий — план текстиля и декора (лист 40); подушки и пледы — по марке мебели.

Допущения и предложения на листе

Основа листа: размеры сняты с растрового плана заказчика без размеров: масштаб восстановлен по площадям помещений (≈ 11,8 мм на пиксель), контрольный обмер не выполнен (К-1); высота потолка 2700 мм принята: на плане заказчика её нет (К-2); толщины стен 300 / 120 мм приняты по плану заказчика, не замерены (К-1); разрешённая мощность 15 кВт принята по типовым ТУ для квартиры, ТУ заказчиком не переданы (К-4).
См. лист открытых вопросов (лист 5, записи К-1, К-2, К-4).

Изм.	Кол.уч	Лист	№ док.	Подп.	Дата
Разраб.		Кырлан А.С.			09.10.26
Пров.					
ГИП					
Н. контр.					
Утв.					

ГД-2026-007-АИ

Квартира 65 м²

Общая площадь 65,24* м² · * размеры со скана, не замерены (реестр — п. 5, К-1)

Дизайн-проект интерьера	Стадия	Лист	Листов
	РП	42	79
Ведомость текстиля М 6/м	Кырлан Александр Сергеевич		

выпуск 09.10.2026 · 147dabfd23 · стр. 52 из 110

Ведомость декора. Схемы развески

ПРЕДВАРИТЕЛЬНО · не для производства работ · открыто пунктов: 4 (реестр — л. 5)


Картины, зеркала, растения, настольный декор · схемы развески (М 1:50) · высоты — мм от чистого пола

Декор: картины, зеркала, растения, предметы


картина · зеркало · мебель под изделием

Поз.	Пом.	Предмет	Размер, мм	Место: стена, высота от пола, мм	Масса, кг	Крепёж и основание	Свет места, отделка	Кол.
ДК3	9	Картина над кроватью	1000×700	стена А, привязка 1560; низ 1300, центр 1650; над С7	4	подвес по основанию, 2 точки	рама — дуб	1
ДК4	9	Зеркало в рост в тонкой чёрной раме	600×1600	стена Г, привязка 700; низ 300, центр 1100	12	анкер для пустотелых оснований, 4 шт.; основание: перегородка — определить обмером до монтажа; нагрузка 30 кг	рама — чёрный матовый металл	1

ДК3 — Детская (пом. 9), стена А (М 1:50)

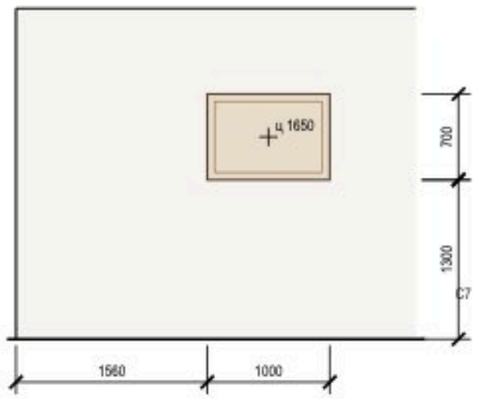

ДК4 — Детская (пом. 9), стена Г (М 1:50)

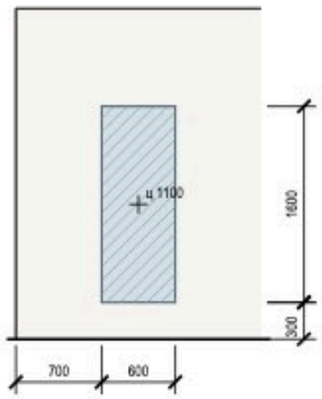

Допущения и предложения на листе

Основа листа: размеры сняты с растрового плана заказчика без размеров: масштаб восстановлен по площадям помещений (≈ 11,8 мм на пиксель), контрольный обмер не выполнен (К-1); высота потолка 2700 мм принята: на плане заказчика её нет (К-2); толщины стен 300 / 120 мм приняты по плану заказчика, не замерены (К-1); разрешённая мощность 15 кВт принята по типовым ТУ для квартиры, ТУ заказчиком не переданы (К-4).

См. лист открытых вопросов (лист 5, записи К-1, К-2, К-4).

Примечания

1. Высоты — от чистого пола помещения до низа изделия, «ц» — до центра; привязки — от чистовой грани угла стены, мм.
2. Над мебелью низ изделия — на 150–250 мм выше спинки или изголовья; без мебели центр — на 1450–1600 мм от пола.
3. Изделия до 5 кг — на два подвеса по основанию; тяжелее — на анкеры с нагрузкой не меньше двойной массы; на ГКЛ — только по закладной или анкеру для пустотелых оснований.
4. Зеркала в рост — с креплением от опрокидывания; в санузлах — влагостойкие, на клей для зеркал и нейтральный силикон.
5. Места изделий — план текстиля и декора (лист 40).

Изм.	Кол.уч	Лист	№ док.	Подп.	Дата
Разраб.		Кырлан А.С.			09.10.26
Пров.					
ГИП					
Н. контр.					
Утв.					

ГД-2026-007-АИ

Квартира 65 м²

Общая площадь 65,24* м² · * размеры со скана, не замерены (реестр — п. 5, К-1)

Дизайн-проект интерьера

Стадия	Лист	Листов
РП	43	79

Ведомость декора. Схемы развески

М 6/м


Кырлан Александр Сергеевич

выпуск 09.10.2026 · 147dabfd23 · стр. 53 из 110

Встроенная мебель. Схема расположения

встроенная и корпусная мебель на заказ, кухонный гарнитур · размеры в мм · марки — по ведомости изделий

ПРЕДВАРИТЕЛЬНО · не для производства работ · открыто пунктов: 4 (реестр — л. 5)

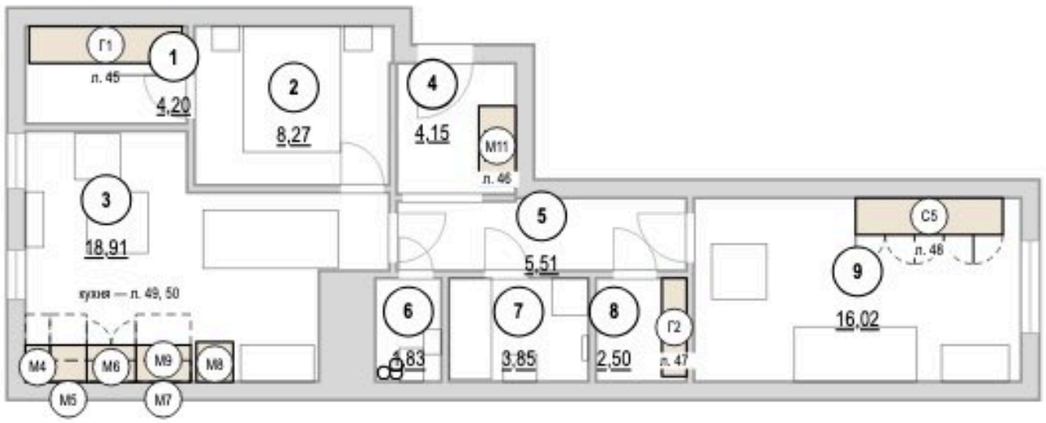

Ведомость изделий

Марка	Наименование	Пом.	Ш×Г×В, мм	Лист
Г1	Система хранения	1	2500×600×2400	45
М11	Шкаф-купе	4	1300×600×2600	46
Г2	Система хранения	8	1600×400×2400	47
С5	Шкаф распашной	9	2400×600×2400	48
М8	Пенал: холодильник	3	600×650×2100	49
М7	Модуль нижний: ящики	3	900×600×900	49
М9	Модуль навесной: полки, сушка	3	2700×350×720	49
М6	Модуль нижний: мойка	3	800×600×900	49
М5	Модуль нижний: ящики, варочная	3	600×600×900	49
М4	Модуль нижний: ящики	3	400×600×900	49

Условные обозначения

- изделие мебельщика: корпус на полу
- навесной модуль (невидимый контур)
- открывание распашного фасада
- зона выдвижения ящика, двери техники
- дверь купе, стрелка — направление движения
- (ПБ) марка изделия, под ней — лист изделия

Примечания

1. Изделия — по чистовым размерам помещений; перед раскроем — контрольный замер цеха после чистовой отделки стен, пола и потолка.
2. Открывание фасадов и выдвижение ящиков показано в открытом положении: зоны не пересекают двери, радиаторы, выключатели и проходы.
3. Стояки и счётчики за мебелью — с сервисным люком; газовые трубы мебелью не зашиваются.
4. Покупная мебель — по плану расстановки мебели и спецификации дизайнера; здесь — подложкой.

Допущения и предложения на листе

Основа листа: размеры сняты с растрового плана заказчика без размеров: масштаб восстановлен по площадям помещений (≈ 11,8 мм на пиксель), контрольный обмер не выполнен (К-1); высота потолка 2700 мм принята: на плане заказчика её нет (К-2); толщины стен 300 / 120 мм приняты по плану заказчика, не замерены (К-1); разрешённая мощность 15 кВт принята по типовым ТУ для квартиры, ТУ заказчиком не переданы (К-4).

См. лист открытых вопросов (лист 5, записи К-1, К-2, К-4).

1000 мм · печать 1:1

Изм.	Кол.уч	Лист	№ док.	Подп.	Дата
Разраб.		Кырпан А.С.			09.10.26
Пров.					
ГИП					
Н. контр.					
Утв.					

ГД-2026-007-АИ

Квартира 65 м²

Общая площадь 65,24* м² · * размеры со скана, не замерены (реестр — п. 5, К-1)

Дизайн-проект интерьера

Стадия	Лист	Листов
РП	44	79

Встроенная мебель. Схема расположения

М 1:100

Кырпан Александр Сергеевич


выпуск 09.10.2026 № 147dabfd23 · стр. 54 из 110

Система хранения Г1


Гардеробная (пом. 1) · вид из помещения · размеры в мм, отметки в м

ПРЕДВАРИТЕЛЬНО · не для производства работ · открыто пунктов: 4 (реестр — л. 5)


Общий вид

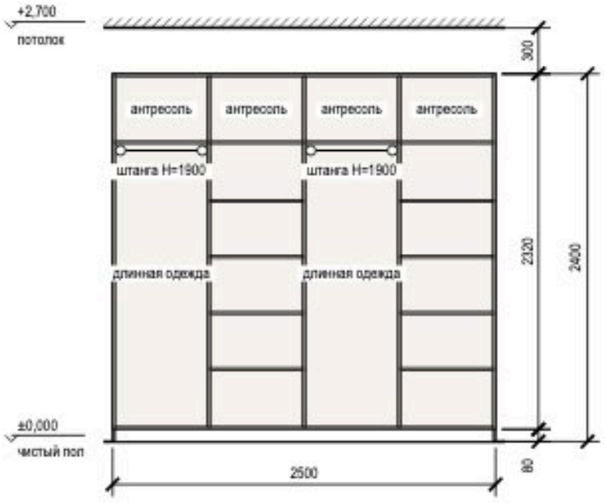


Наполнение, размеры в свету

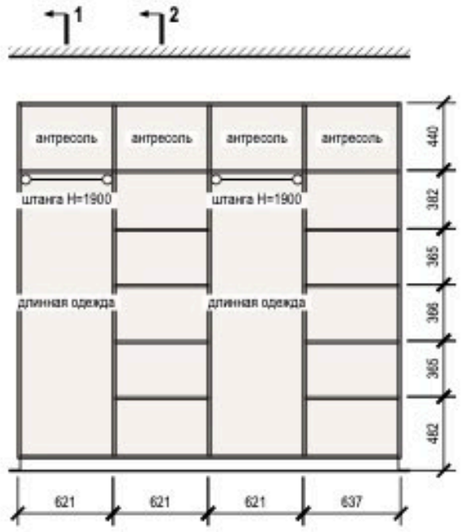

Разрез 1-1

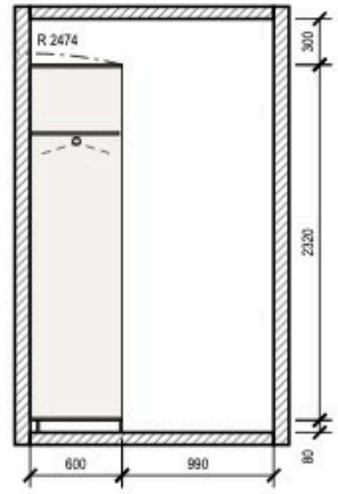

Разрез 2-2

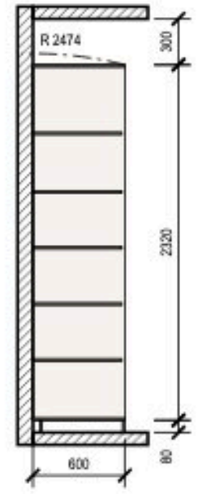

Примечания

1. Размеры — в мм по чистовой отделке; изделие 2500×600×2400 (Ш×Г×В). Перед раскроем — контрольный замер цеха после чистовой отделки стен, пола и потолка.
2. Корпус — ЛДСП 16 мм, задняя стенка ХДФ 4 мм в паз, цоколь 80 мм на регулируемых опорах; открытая система без фасадов, ящики с фасадами.
3. Кромка: скрытые торцы 0,4 мм, видимые 2 мм (ПВХ/АБС).
4. Номинальные зазоры: между фасадами ящиков 3 мм, фасад ящика — стойка 2 мм.
5. Ящики — направляющие полного выдвижения NL 550 (внутренняя глубина 596 мм ≥ NL + 3); присадка по 32-й системе — выполняет цех.
6. Зазор до потолка 300 мм.
7. Подъём корпуса: диагональ боковины √(2400² + 600²) = 2474 мм < 2700 мм до потолка — корпус собирается лёжа и поднимается поворотом.
8. Крепление к стене от опрокидывания: крепление к стене, 3 точки; основание стены и шаг анкеров — монтажная схема шкафов.
9. Проход перед изделием 990 мм показан на разрезе 1-1.

Условные обозначения

- корпус и полки ЛДСП (вид на стену)
- задняя стенка ХДФ
- деталь в разрезе
- штанга для плечиков (на разрезе — плечики 450 мм)
- траектория угла корпуса при подъёме в проектное положение

Допущения и предложения на листе

Основа листа: размеры сняты с растрового плана заказчика без размеров: масштаб восстановлен по площадям помещений (≈ 11,8 мм на пиксель), контрольный обмер не выполнен (К-1); высота потолка 2700 мм принята: на плане заказчика её нет (К-2); толщины стен 300 / 120 мм приняты по плану заказчика, не замерены (К-1); разрешённая мощность 15 кВт принята по типовым ТУ для квартиры, ТУ заказчиком не переданы (К-4).

См. лист открытых вопросов (лист 5, записи К-1, К-2, К-4).

1000 мм · печать 1:1

						ГД-2026-007-АИ	
						Квартира 65 м²	
Изм.	Кол.уч	Лист	№ док.	Подп.	Дата	Общая площадь 65,24* м² · * размеры со скана, не замерены (реестр — п. 5, К-1)	
Разраб.		Кырпан А.С.			09.10.26	Дизайн-проект интерьера	Стадия: РП; Лист: 45; Листов: 79
Пров.							
ГИП						Система хранения Г1	Кырпан Александр Сергеевич
						М 1:40	
Н. контр.							
Утв.							


выпуск 09.10.2026 № 147dabfd23 · стр. 55 из 110

Шкаф-купе М11


Прихожая (пом. 4) · вид из помещения · размеры в мм, отметки в м

ПРЕДВАРИТЕЛЬНО · не для производства работ · открыто пунктов: 4 (реестр — л. 5)


Вид с фасадами

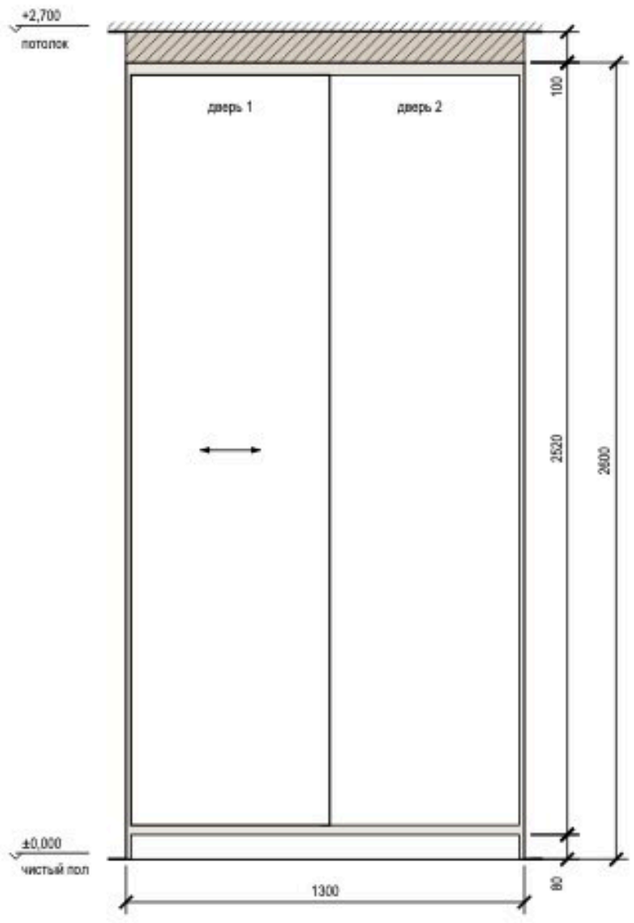


Вид без фасадов

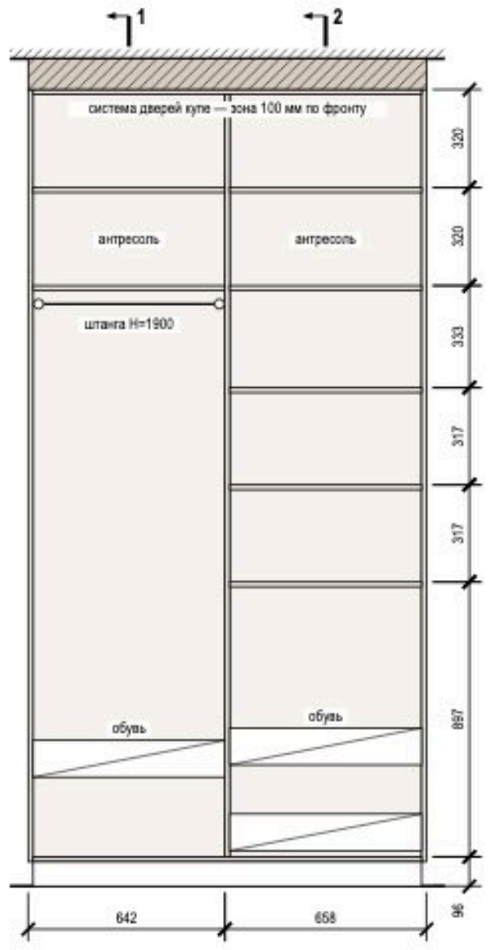

Разрез 1-1

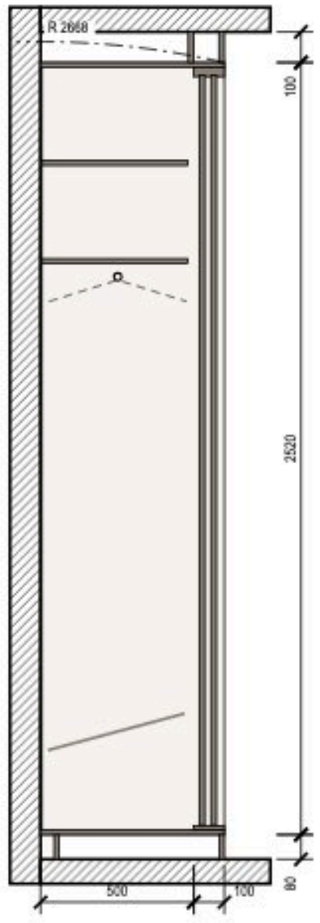

Разрез 2-2

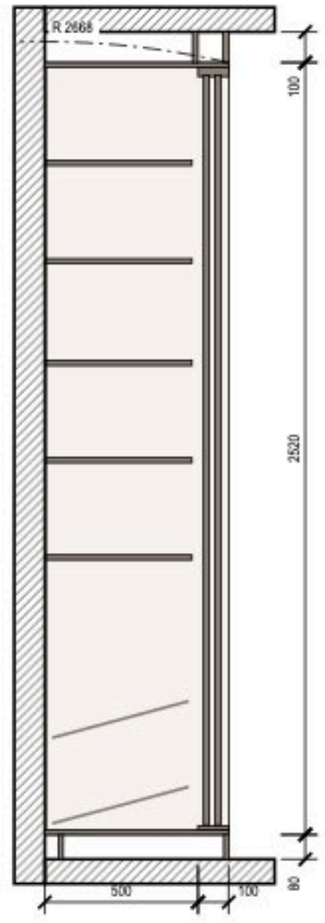

Примечания

1. Размеры — в мм по чистовой отделке; изделие 1300×600×2600 (Ш×Г×В). Перед раскроем — контрольный замер цеха после чистовой отделки стен, пола и потолка.
2. Корпус — ЛДСП 16 мм, задняя стенка ХДФ 4 мм в паз, цоколь 80 мм на регулируемых опорах; двери купе — ЛДСП 10 мм в алюминиевом профиле, нахлёст 30 мм, ширина двери 649 мм, высота — проём минус 40 мм; цвет — по колерной карте.
3. Кромка: скрытые торцы 0,4 мм, видимые 1 мм (ПВХ/АБС).
4. Номинальные зазоры: дверь купе — боковина 3 мм, фасад ящика — стойка 2 мм; ящики внутри купе — с накладкой 30 мм на стойке со стороны нахлёста дверей.
5. Ящики — направляющие полного выдвижения NL 450 (внутренняя глубина 496 мм ≥ NL + 3); присадка по 32-й системе — выполняет цех.
6. Компенсатор 100 мм — короб из ЛДСП по фронту и торцам, подгоняется к потолку при монтаже (припуск 20 мм), крепится к корпусу и к потолку.
7. Подъём корпуса: диагональ боковины √(2600² + 600²) = 2668 мм < 2700 мм до потолка — корпус собирается лёжа и поднимается поворотом.
8. Крепление к стене от опрокидывания — уголки 2 шт. к несущему основанию (монтажная схема шкафов).

Условные обозначения

- дверь купе, стрелка — направление движения
- корпус и полки ЛДСП (вид на стену)
- задняя стенка ХДФ
- деталь в разрезе
- компенсатор — короб до потолка
- штанга для плечиков (на разрезе — плечики 450 мм)
- траектория угла корпуса при подъёме в проектное положение

Допущения и предложения на листе

Основа листа: размеры сняты с растрового плана заказчика без размеров: масштаб восстановлен по площадям помещений (≈ 11,8 мм на пиксель), контрольный обмер не выполнен (К-1); высота потолка 2700 мм принята: на плане заказчика её нет (К-2); толщины стен 300 / 120 мм приняты по плану заказчика, не замерены (К-1); разрешённая мощность 15 кВт принята по типовым ТУ для квартиры, ТУ заказчиком не переданы (К-4).

См. лист открытых вопросов (лист 5, записи К-1, К-2, К-4).

1000 мм · печать 1:1

Изм.	Кол.уч	Лист	№ док.	Подп.	Дата
Разраб.		Кырпан А.С.			09.10.26
Пров.					
ГИП					
Н. контр.					
Утв.					

ГД-2026-007-АИ

Квартира 65 м²

Общая площадь 65,24* м² · * размеры со скана, не замерены (реестр — п. 5, К-1)

Дизайн-проект интерьера

Стадия	Лист	Листов
РП	46	79

Шкаф-купе М11

М 1:20

Кырпан Александр Сергеевич


выпуск 09.10.2026 № 147dabfd23 · стр. 56 из 110

Система хранения Г2


Кладовая (пом. 8) · вид из помещения · размеры в мм, отметки в м

ПРЕДВАРИТЕЛЬНО · не для производства работ · открыто пунктов: 4 (реестр — л. 5)


Общий вид

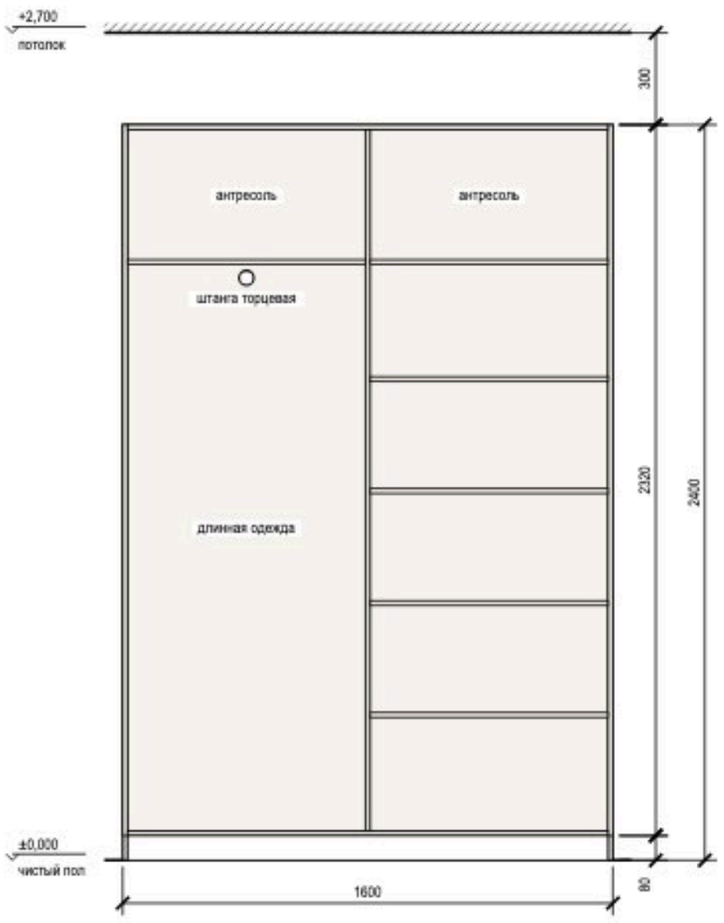


Наполнение, размеры в свету

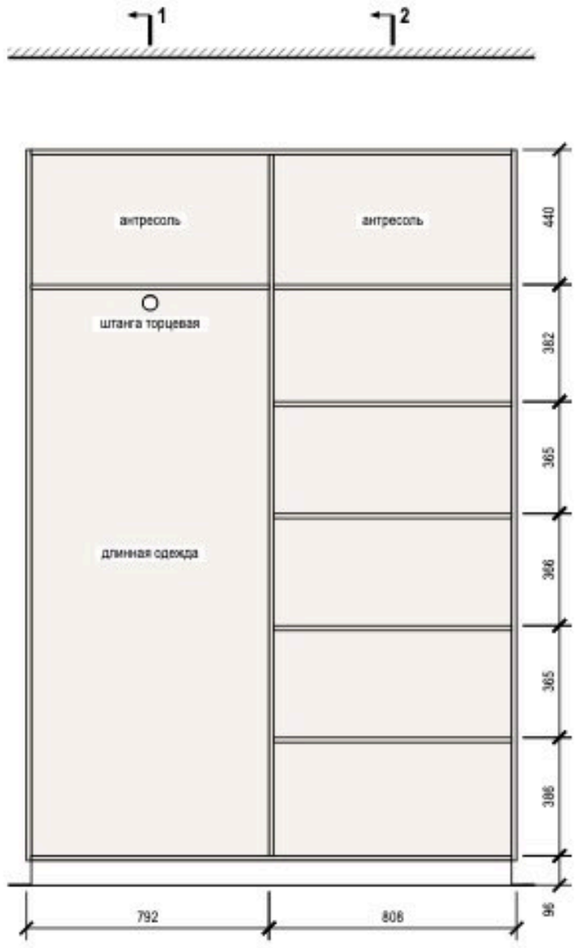

Разрез 1-1

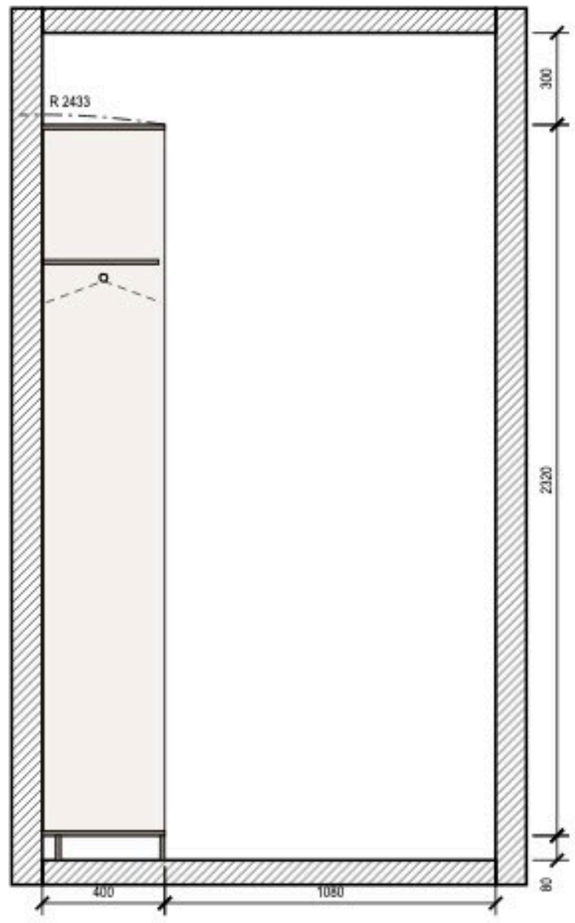

Разрез 2-2

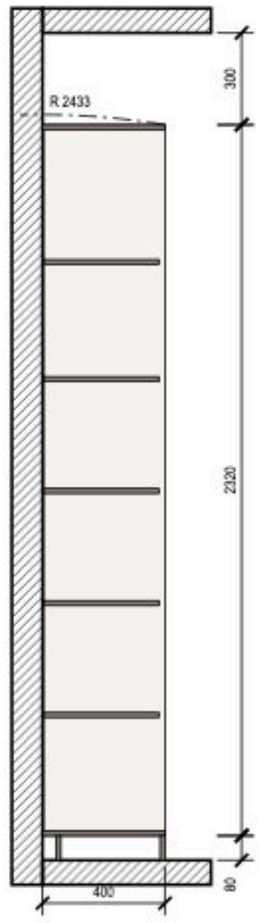

Примечания

1. Размеры — в мм по чистовой отделке; изделие 1600×400×2400 (Ш×Г×В). Перед раскроем — контрольный замер цеха после чистовой отделки стен, пола и потолка.
2. Корпус — ЛДСП 16 мм, задняя стенка ХДФ 4 мм в паз, цоколь 80 мм на регулируемых опорах; открытая система без фасадов, ящики с фасадами.
3. Кромка: скрытые торцы 0,4 мм, видимые 2 мм (ПВХ/АБС).
4. Номинальные зазоры: между фасадами ящиков 3 мм, фасад ящика — стойка 2 мм.
5. Ящики — направляющие полного выдвижения NL 350 (внутренняя глубина 396 мм ≥ NL + 3); присадка по 32-й системе — выполняет цех.
6. Зазор до потолка 300 мм.
7. Подъём корпуса: диагональ боковины √(2400² + 400²) = 2433 мм < 2700 мм до потолка — корпус собирается лёжа и поднимается поворотом.
8. Крепление к стене от опрокидывания — уголки 2 шт. к несущему основанию (монтажная схема шкафов).
9. Проход перед изделием 1080 мм показан на разрезе 1-1.

Условные обозначения

- корпус и полки ЛДСП (вид на стену)
- задняя стенка ХДФ
- деталь в разрезе
- штанга для плечиков (на разрезе — плечики 450 мм)
- траектория угла корпуса при подъёме в проектное положение

Допущения и предложения на листе

Основа листа: размеры сняты с растрового плана заказчика без размеров: масштаб восстановлен по площадям помещений (≈ 11,8 мм на пиксель), контрольный обмер не выполнен (К-1); высота потолка 2700 мм принята: на плане заказчика её нет (К-2); толщины стен 300 / 120 мм приняты по плану заказчика, не замерены (К-1); разрешённая мощность 15 кВт принята по типовым ТУ для квартиры, ТУ заказчиком не переданы (К-4).

См. лист открытых вопросов (лист 5, записи К-1, К-2, К-4).

1000 мм · печать 1:1

Изм.	Кол.уч	Лист	№ док.	Подп.	Дата
Разраб.		Кырлан А.С.			09.10.26
Пров.					
ГИП					
Н. контр.					
Утв.					

ГД-2026-007-АИ

Квартира 65 м²

Общая площадь 65,24* м² · * размеры со скана, не замерены (реестр — п. 5, К-1)

Дизайн-проект интерьера

Стадия	Лист	Листов
РП	47	79

Система хранения Г2

М 1:20

Кырлан Александр Сергеевич


выпуск 09.10.2026 · 147dabfd23 · стр. 57 из 110

Шкаф распашной С5


Детская (пом. 9) · вид из помещения · размеры в мм, отметки в м

ПРЕДВАРИТЕЛЬНО · не для производства работ · открыто пунктов: 4 (реестр — л. 5)


Вид с фасадами

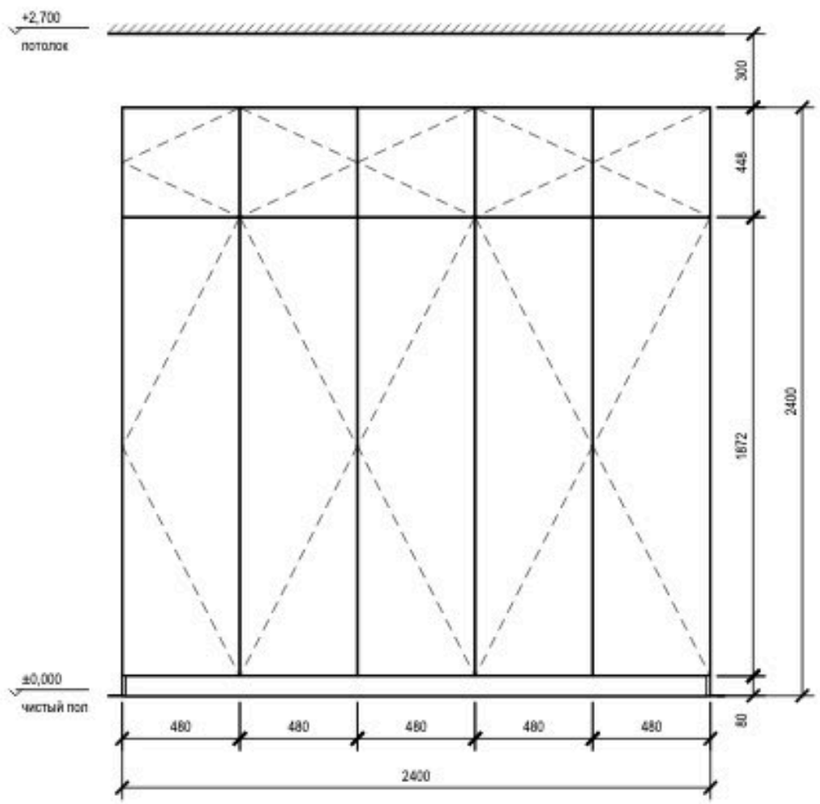


Вид без фасадов

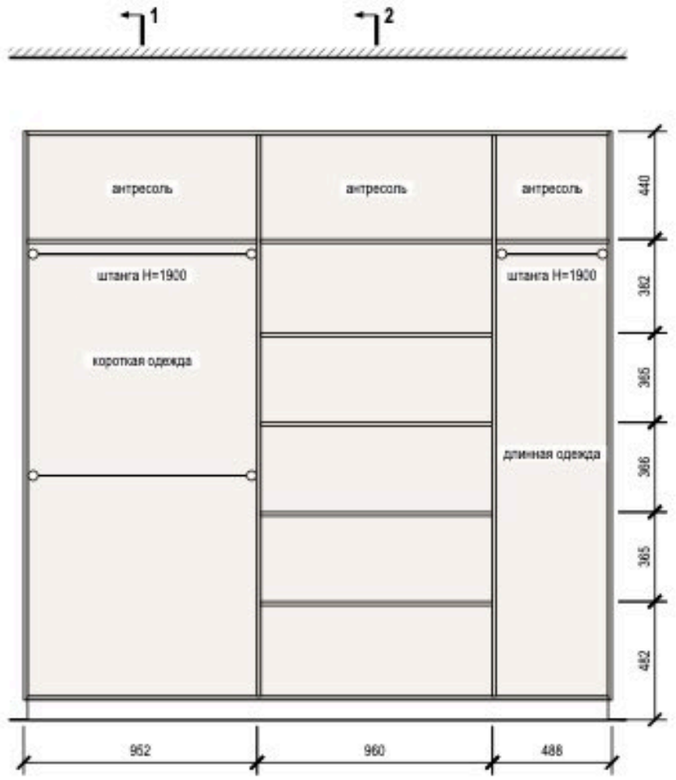

Разрез 1-1

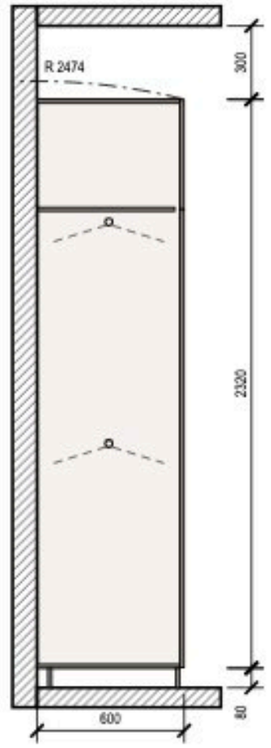

Разрез 2-2

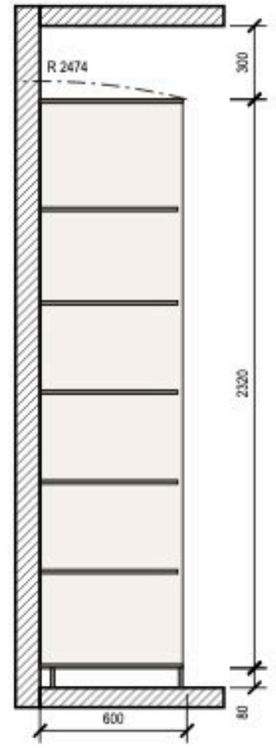

Примечания

1. Размеры — в мм по чистовой отделке; изделие 2400×600×2400 (Ш×Г×В). Перед раскроем — контрольный замер цеха после чистовой отделки стен, пола и потолка.
2. Корпус — ЛДСП 16 мм, задняя стенка ХДФ 4 мм в паз, цоколь 80 мм на регулируемых опорах; фасады — МДФ, эмаль матовая 18 мм накладные, цвет — по колерной карте; петли с доводчиком: фасад 1869 мм — 4 петли, фасад 445 мм — 2 петли.
3. Кромка: скрытые торцы 0,4 мм, видимые 2 мм (ПВХ/АБС).
4. Номинальные зазоры: между фасадами 3 мм, фасад — стена и фасад — потолок не менее 3 мм, фасад ящика — стойка 2 мм.
5. Ящики — направляющие полного выдвижения NL 550 (внутренняя глубина 578 мм ≥ NL + 3); присадка по 32-й системе — выполняет цех.
6. Зазор до потолка 300 мм.
7. Подъём корпуса: диагональ боковины √(2400² + 600²) = 2474 мм < 2700 мм до потолка — корпус собирается лёжа и поднимается поворотом.
8. Крепление к стене от опрокидывания — уголки 2 шт. к несущему основанию (монтажная схема шкафов).

Условные обозначения

- фасад распашной: линии сходятся к стороне петель
- корпус и полки ЛДСП (вид на стену)
- задняя стенка ХДФ
- деталь в разрезе
- штанга для плечиков (на разрезе — плечики 450 мм)
- траектория угла корпуса при подъёме в проектное положение

Допущения и предложения на листе

Основа листа: размеры сняты с растрового плана заказчика без размеров: масштаб восстановлен по площадям помещений (≈ 11,8 мм на пиксель), контрольный обмер не выполнен (К-1); высота потолка 2700 мм принята: на плане заказчика её нет (К-2); толщины стен 300 / 120 мм приняты по плану заказчика, не замерены (К-1); разрешённая мощность 15 кВт принята по типовым ТУ для квартиры, ТУ заказчиком не переданы (К-4).

См. лист открытых вопросов (лист 5, записи К-1, К-2, К-4).

1000 мм · печать 1:1

Изм.	Кол.уч	Лист	№ док.	Подп.	Дата
Разраб.		Кырпан А.С.			09.10.26
Пров.					
ГИП					
Н. контр.					
Утв.					

ГД-2026-007-АИ

Квартира 65 м²

Общая площадь 65,24* м² · * размеры со скана, не замерены (реестр — п. 5, К-1)

Дизайн-проект интерьера

Стадия	Лист	Листов
РП	48	79

Шкаф распашной С5

М 1:25

Кырпан Александр Сергеевич


выпуск 09.10.2026 · 147dabfd23 · стр. 58 из 110

Кухня (пом. 3). Развёртка гарнитура


Кухня-гостиная (пом. 3) · стена В · вид из помещения · размеры в мм, отметки в м

ПРЕДВАРИТЕЛЬНО · не для производства работ · открыто пунктов: 4 (реестр — л. 5)


Вид с фасадами

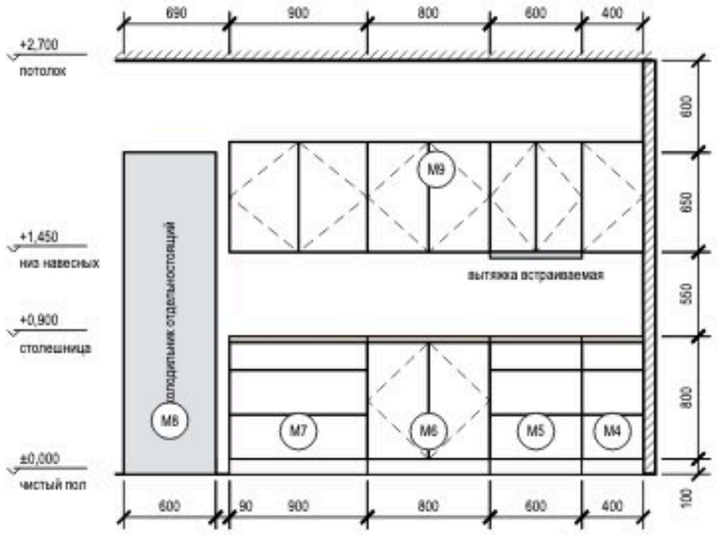


Вид без фасадов (наполнение, выводы)

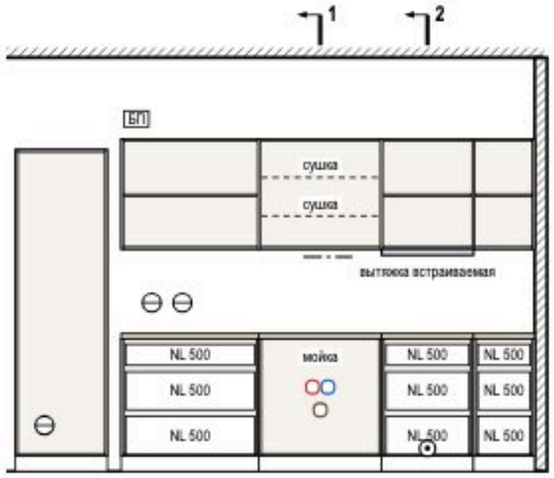

Разрез 1-1

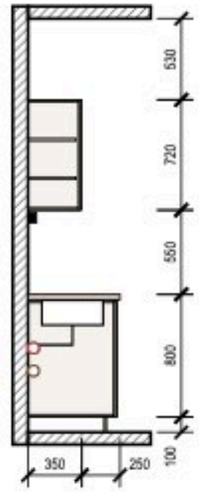

Разрез 2-2

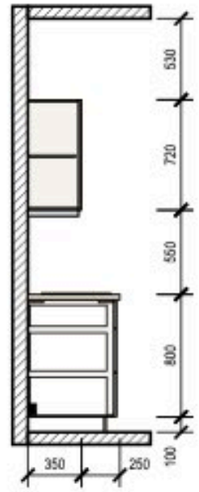

Условные обозначения

- фасад распашной: линии сходятся к стороне петель
- фасад ящика, карго
- встраиваемая техника
- столешница
- доборная планка
- деталь в разрезе
- K1 — марка модуля
- розетка на стене
- вывод кабеля к технике
- B1 — вывод воды В1 / Т3, канализации К1

Примечания

1. Размеры — в мм по чистовой отделке, вид из помещения; марки — как на плане расстановки. Перед раскроем — контрольный замер цеха после фартука и пола.
2. Корпуса — ЛДСП 16 мм, задняя стенка ХДФ 4 мм; фасады — МДФ эмаль 18 мм, цвет по колерной карте; столешница 38 мм, свес 20 мм; цоколь 100 мм.
3. Кромка: скрытые торцы 0,4 мм, видимые 1 мм. Номинальные зазоры: между фасадами 3 мм, фасад — столешница 3 мм, фасад — стена не менее 3 мм.
4. Ящики полного выдвижения и петли — с доводчиком; присадка по 32-й системе — выполняет цех.
5. Вытяжка встраивается в навесной модуль над варочной: её низ 510 мм над панелью — меньше 650 мм, модуль поднять или принять вытяжку с допуском по паспорту модели.
6. Ниши техники — по монтажным схемам выбранных моделей: решётка в цоколе и канал за пеналом холодильника, зазор за духовым шкафом, фасад ПММ на двери машины.

Допущения и предложения на листе

Основа листа: размеры сняты с растрового плана заказчика без размеров: масштаб восстановлен по площадям помещений (≈ 11,8 мм на пиксель), контрольный обмер не выполнен (К-1); высота потолка 2700 мм принята: на плане заказчика её нет (К-2); толщины стен 300 / 120 мм приняты по плану заказчика, не замерены (К-1); разрешённая мощность 15 кВт принята по типовым ТУ для квартиры, ТУ заказчиком не переданы (К-4).

См. лист открытых вопросов (лист 5, записи К-1, К-2, К-4).

1000 мм · печать 1:1

Изм.	Кол.уч	Лист	№ док.	Подп.	Дата
Разраб.		Кырпан А.С.			09.10.26
Пров.					
ГИП					
Н. контр.					
Утв.					

ГД-2026-007-АИ

Квартира 65 м²

Общая площадь 65,24* м² · * размеры со скана, не замерены (реестр — п. 5, К-1)

Дизайн-проект интерьера

Стадия	Лист	Листов
РП	49	79

Кухня (пом. 3). Развёртка гарнитура

М 1:40


Кырпан Александр Сергеевич

выпуск 09.10.2026 № 147dabfd23 · стр. 59 из 110


Кухня (пом. 3). Монтажная схема

Кухня-гостиная (пом. 3) · стена В · размеры в мм от чистых поверхностей, высоты — от чистого пола

Привязка выводов и крепление модулей

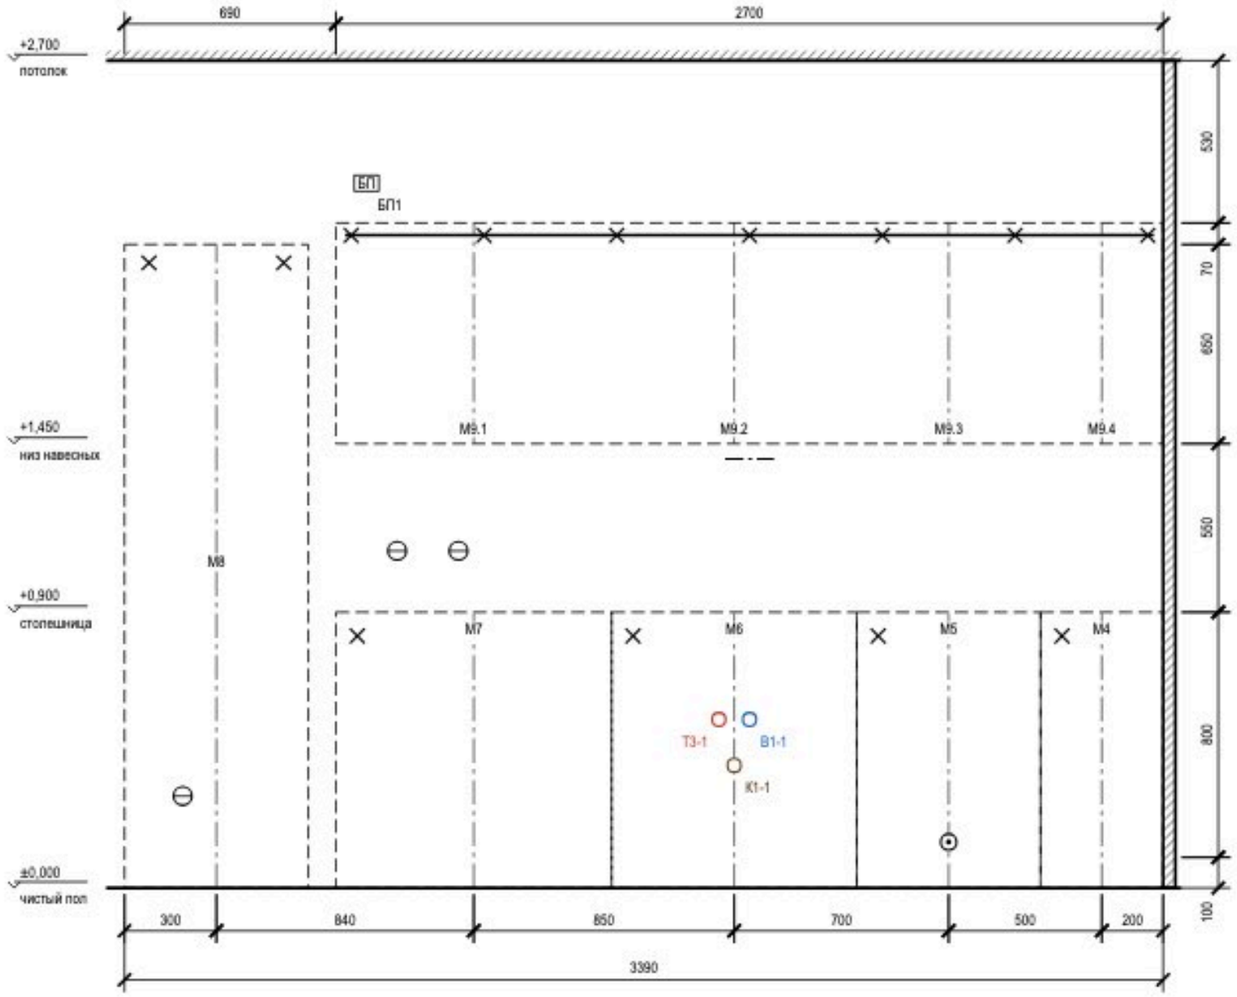

План столешницы

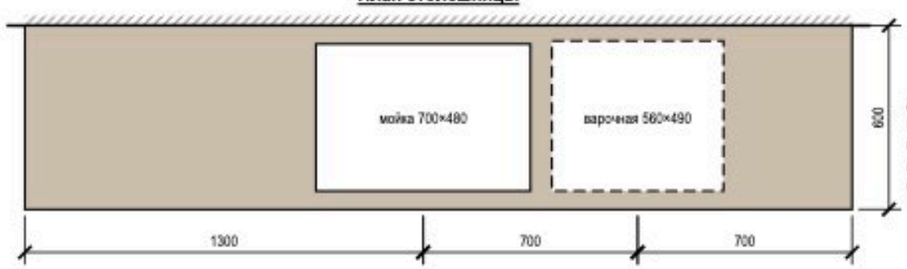

Привязка выводов к осям модулей

Код	Назначение	Модуль	От оси, мм	H, мм	Размещение
	розетка — холодильник	М8	−110	300	за пеналом
БП1	блок питания	М9.1	−350	2300	в навесном модуле
	розетка — рабочая зона	М7	−250	1100	над столешницей (фартук)
	розетка ×2 — рабочая зона	М7	−50	1100	над столешницей (фартук)
Т3-1	Т3 — межос. 100	М6	−50	550	в модуле мойки
К1-1	К1 Ø50 — мойка	М6	0	400	в модуле мойки
	светодиодная лента — подсветка столешницы	М6	+50	1400	в профиле по низу навесного модуля
В1-1	В1 — межос. 100	М6	+50	550	в модуле мойки
	вывод кабеля — варочная панель	М5	0	150	в соседнем модуле, за ящиком

Зазоры под отделку

Поверхность	Отделка	Зазор, мм	Учесть
фартук	плитка / стеновая панель	10	от чернового основания до корпуса навесных и столешницы
стены	окраска	5	под штукатурку и шпаклёвку за пеналом
пол	инженерная доска		цоколь — после укладки пола, опоры ±20 мм

Условные обозначения

- навесной модуль (невидимый контур)
- ось модуля (от неё — привязка вывода)
- анкер / уголок крепления к стене
- розетка на стене
- вывод кабеля к технике
- В1 — вывод воды В1 / Т3, канализации К1

Допущения и предложения на листе

Основа листа: размеры сняты с растрового плана заказчика без размеров: масштаб восстановлен по площадям помещений (≈ 11,8 мм на пиксель), контрольный обмер не выполнен (К-1); высота потолка 2700 мм принята: на плане заказчика её нет (К-2); толщины стен 300 / 120 мм приняты по плану заказчика, не замерены (К-1); разрешённая мощность 15 кВт принята по типовым ТУ для квартиры, ТУ заказчиком не переданы (К-4).
См. лист открытых вопросов (лист 5, записи К-1, К-2, К-4).

Примечания

1. Выводы — по проекту электрики и ВК; привязка по горизонтали — от оси модуля (плюс — вправо по виду), по высоте — от чистого пола до оси вывода.
2. Пенал — уголки к стене 2 шт. сверху; нижние модули — стяжками между собой и уголком к стене; ряд выставить по уровню опорами цоколя.
3. Розетки над столешницей — не ниже 150 мм над ней и не за корпусом техники; розетка за ПММ, духовым шкафом и холодильником — только в соседнем модуле или в зоне цоколя с доступом.
4. Столешница — вырезы по шаблонам выбранных моделей мойки и варочной панели; торцы у стены — герметик, пристеночный плинтус.

1000 мм · печать 1:1

Изм.	Кол.уч	Лист	№ док.	Подп.	Дата
Разраб.		Кырпан А.С.			09.10.26
Пров.					
ГИП					
Н. контр.					
Утв.					

ГД-2026-007-АИ

Квартира 65 м²

Общая площадь 65,24* м² · * размеры со скана, не замерены (реестр — п. 5, К-1)

Дизайн-проект интерьера

Стадия	Лист	Листов
РП	50	79

Кухня (пом. 3). Монтажная схема

М 1:20


Кырпан Александр Сергеевич

выпуск 09.10.2026 № 147dabfd23 · стр. 60 из 110


Шкафы. Монтажная схема

крепление к стене, установочные размеры, зазоры под отделку · размеры в мм


Система хранения Г1 (пом. 1)

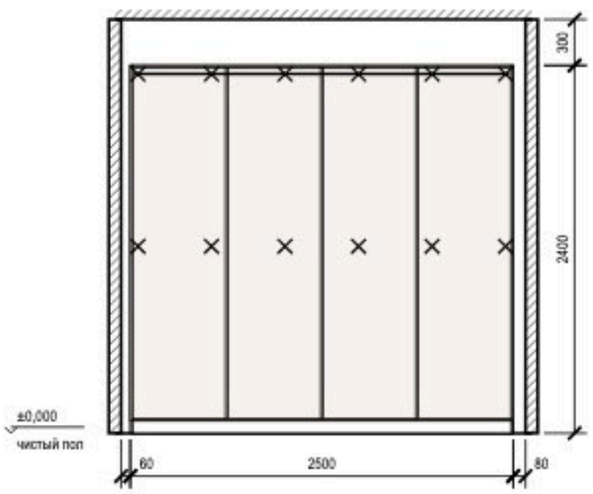


Шкаф-купе М11 (пом. 4)

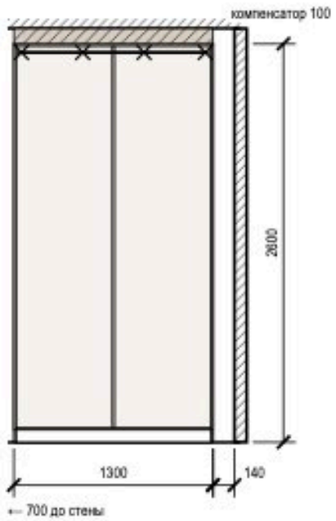

Система хранения Г2 (пом. 8)

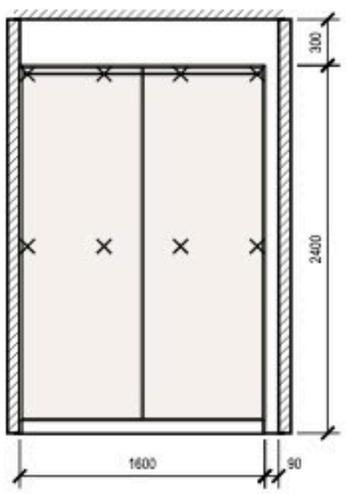

Шкаф распашной С5 (пом. 9)

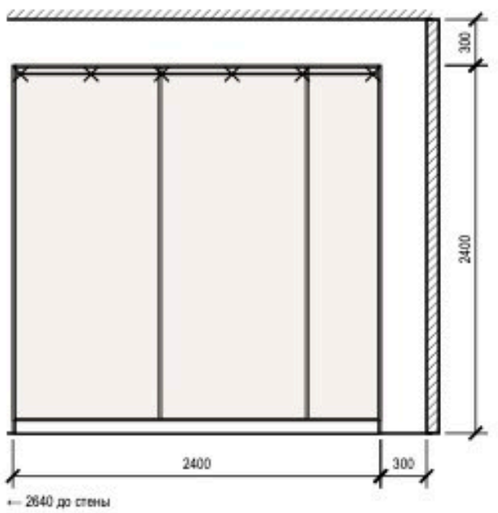

Крепление и зазоры под отделку

Марка	Помещение, стена	Основание	Отделка стены	Зазор, мм	Крепёж по плане	От опрокидывания
Г1	Гардеробная (1), стена А	по основанию — см. таблицу крепежа	окраска	5	анкер 12 шт. (2 ряда)	крепление к стене, 3 точки
М11	Прихожая (4), стена Б	по основанию — см. таблицу крепежа	окраска	5	анкер 4 шт., шаг 400	уголки 2 шт.
Г2	Кладовая (8), стена Б	по основанию — см. таблицу крепежа	окраска	5	анкер 8 шт. (2 ряда)	уголки 2 шт.
С5	Детская (9), стена А	по основанию — см. таблицу крепежа	окраска	5	анкер 6 шт., шаг 460	уголки 2 шт.

Крепёж по основанию стены

Основание стены	Крепёж
бетон, ж/б	анкер-шуруп 7,5×72 или дюбель 8×60 с шурупом 5×70
кирпич полнотелый	дюбель 8×80 с шурупом 5×90
газобетон, пазогребень	дюбель для газобетона 10×100 или химический анкер
гипсокартон	закладная до обшивки (брус 40×80 или фанера 18 мм), саморез в закладную

Условные обозначения

- × — анкер / уголок крепления к стене
- прямоугольник — корпус и полки ЛДСП (вид на стену)
- штриховка — компенсатор — короб до потолка

Примечания

1. Установочные размеры — от чистого пола и чистых стен; перед установкой контрольный замер после отделки.
2. Порядок: корпус выставить по уровню опорами цоколя → закрепить к стене по задней планке → навесить двери и фасады, отрегулировать зазоры → подогнать и закрепить компенсатор.
3. Анкеры — с шагом не более 500 мм, не ближе 50 мм от края планки; на ГКЛ только в закладную, установленную до обшивки.
4. Скрытые коммуникации под анкеры проверить детектором; трассы электрики по плану розеток.

Допущения и предложения на листе

Основа листа: размеры сняты с растрового плана заказчика без размеров: масштаб восстановлен по площадям помещений (≈ 11,8 мм на пиксель), контрольный обмер не выполнен (К-1); высота потолка 2700 мм принята: на плане заказчика её нет (К-2); толщины стен 300 / 120 мм приняты по плану заказчика, не замерены (К-1); разрешённая мощность 15 кВт принята по типовым ТУ для квартиры, ТУ заказчиком не переданы (К-4).

См. лист открытых вопросов (лист 5, записи К-1, К-2, К-4).

1000 мм · печать 1:1

Изм.	Кол.уч	Лист	№ док.	Подп.	Дата
Разраб.		Кырпан А.С.			09.10.26
Пров.					
ГИП					
Н. контр.					
Утв.					

ГД-2026-007-АИ

Квартира 65 м²

Общая площадь 65,24* м² · * размеры со скана, не замерены (реестр — п. 5, К-1)

Дизайн-проект интерьера

Стадия	Лист	Листов
РП	51	79

Шкафы. Монтажная схема

М 1:40

Кырпан Александр Сергеевич

выпуск 09.10.2026 · 147dabfd23 · стр. 61 из 110

Ведомости изделий, техники и фурнитуры

встроенная мебель и кухонный гарнитур · размеры в мм

Ведомость изделий

Марка	Наименование	Пом.	Ш×Г×В, мм	Корпус	Фасад	Кромка, мм скр./вид.	Кол.
Г1	Система хранения	1	2500×600×2400	ЛДСП 16	без фасадов; ящики — МДФ 18, эмаль матовая	0,4 / 2	1
М11	Шкаф-купе	4	1300×600×2600	ЛДСП 16	рифлёные панели МДФ в алюминиевом профиле	0,4 / 1	1
Г2	Система хранения	8	1600×400×2400	ЛДСП 16	без фасадов; ящики — МДФ 18, эмаль матовая	0,4 / 2	1
С5	Шкаф распашной	9	2400×600×2400	ЛДСП 16	МДФ 18, эмаль матовая	0,4 / 2	1
М8	Пенал: холодильник	3	600×650×2100	ЛДСП 16	МДФ эмаль	0,4 / 1	1
М7	Модуль нижний: ящики	3	900×600×900	ЛДСП 16	МДФ эмаль	0,4 / 1	1
М9	Модуль навесной: полки, сушка	3	2700×350×720	ЛДСП 16	МДФ эмаль	0,4 / 1	1
М6	Модуль нижний: мойка	3	800×600×900	ЛДСП 16	МДФ эмаль	0,4 / 1	1
М5	Модуль нижний: ящики, варочная	3	600×600×900	ЛДСП 16	МДФ эмаль	0,4 / 1	1
М4	Модуль нижний: ящики	3	400×600×900	ЛДСП 16	МДФ эмаль	0,4 / 1	1

Ведомость встраиваемой техники

Поз.	Прибор	Ниша, вырез, мм	Вентиляция	Питание	Схема
М8	Холодильник отдельностоящий	проём 600, зазор сверху ≥ 50	по паспорту модели	розетка рядом, не за корпусом	по модели
М6	Мойка врезная / подстольная с сифоном	вырез по шаблону, ориентир 700 × 480		смеситель — выводы ВК	по модели
М5	Варочная панель индукционная, 60 см	вырез в столешнице 560 × 490		вывод кабеля под модулем	по модели
М5	Вытяжка настенная, 60 см	низ ≥ 650 над панелью	воздуховод к вентканалу, короб до потолка	вывод кабеля в коробе	по модели

Ведомость фурнитуры

№	Фурнитура	Тип, размер	Изделия	Кол.
1	Полкодержатель с фиксацией	ø5 мм	Г1, М11, Г2, С5, М9	140
2	Штанга овальная 30×15, L = 605	+ 2 держателя	Г1	2
3	Опора регулируемая с цоколем на клипсах	ход 20 мм	Г1, М11, Г2, С5	30
4	Анкер по основанию стены	по таблице крепежа	Г1, М11, Г2, С5, М9	37
5	Уголок крепления к стене от опрокидывания	стальной	Г1, М11, Г2, С5, М8	10
6	Система дверей купе: профиль, направляющие, ролики	на 2 двери	М11	1
7	Ручка-профиль вертикальная	в цвет профиля	М11	2
8	Штанга овальная 30×15, L = 626	+ 2 держателя	М11	1
9	Полка для обуви выдвижная наклонная	ширина 626	М11	3
10	Штанга выдвижная торцевая	L по глубине	Г2	1
11	Петля накладная 110° с доводчиком	чашка 35 мм	С5, М9, М6	48
12	Штанга овальная 30×15, L = 936	+ 2 держателя	С5	2
13	Штанга овальная 30×15, L = 456	+ 2 держателя	С5	1
14	Опора кухонная регулируемая 100–120 мм	+ клипса цоколя	М8, М7, М6, М5, М4	24
15	Направляющие полного выдвижения с доводчиком NL 500	пара	М7, М5, М4	9
16	Ручка-профиль	латунь матовая	М7, М9, М6, М5, М4	18
17	Сушка для посуды в шкаф	ширина 800	М9	1
18	Навес регулируемый для навесного шкафа	пара на секцию	М9	4
19	Шина монтажная	L = 2640	М9	1

Примечания

1. Модели техники выбирает заказчик до изготовления мебели; ниши, вырезы и вентиляция — по монтажной схеме выбранной модели (условие гарантии), её номер вносится в ведомость.
2. Количество фурнитуры — по чертежам изделий; запас крепежа 5 %. Аналоги — по характеристикам (доводчик, нагрузка, ход).
3. Цвет корпусов, фасадов и профилей — по колерной карте проекта.

Допущения и предложения на листе

Основа листа: размеры сняты с растрового плана заказчика без размеров: масштаб восстановлен по площадям помещений (≈ 11,8 мм на пиксель), контрольный обмер не выполнен (К-1); высота потолка 2700 мм принята: на плане заказчика её нет (К-2); толщины стен 300 / 120 мм приняты по плану заказчика, не замерены (К-1); разрешённая мощность 15 кВт принята по типовым ТУ для квартиры, ТУ заказчиком не переданы (К-4).

См. лист открытых вопросов (лист 5, записи К-1, К-2, К-4).

Изм.	Кол.уч	Лист	№ док.	Подп.	Дата
Разраб.		Кырпан А.С.			09.10.26
Пров.					
ГИП					
Н. контр.					
Утв.					

ГД-2026-007-АИ

Квартира 65 м²

Общая площадь 65,24* м² · * размеры со скана, не замерены (реестр — п. 5, К-1)

Дизайн-проект интерьера	Стадия	Лист	Листов
	РП	52	79

Ведомости изделий, техники и фурнитуры	Кырпан Александр Сергеевич
М 6/м	

выпуск 09.10.2026 № 147dabfd23 · стр. 62 из 110

09

Развёртки и узлы

Кырлан Александр Сергеевич

выпуск 09.10.2026 № 147dabfd23 · стр. 63 из 110

Реестр марок отделки и позиций альбома

Реестр марок отделки (О ↔ позиции колерной карты) и марки позиций по видам

Реестр марок отделки альбома

Марка	Поверхность	Материал, изделие	Цвет, код	Помещения	Колер. карта
О1	стены	окраска, Tikkurila Harmony, матовая, подготовка Q3	Tikkurila V503 «Winter»	1	К1
О2	плинтус	плинтус МДФ, Orac Decor Contour (Luxxus), h 69 мм, SX165	Tikkurila V503 «Winter»	1	К3
О3	потолок	окраска, Tikkurila Anti-Reflex 2, глубокоматовая, подготовка Q3	Tikkurila V503 «Winter»	1, 9	К2
О4	пол	инженерная доска, Quick-Step Impressive, 1380×190 мм, IM1848		1, 2, 3, 8, 9	КМ1
О5	стены	окраска, Tikkurila, глубокоматовая, подготовка Q3	NCS S 1502-Y50R	2, 4, 5	К4, К9
О6	плинтус	плинтус МДФ, Orac Decor Contour (Luxxus), h 69 мм, SX165, шелковисто-матовая	NCS S 0300-N	2, 3, 4, 5, 8	К6
О7	потолок	окраска, Tikkurila, глубокоматовая	NCS S 0300-N	2, 3, 4, 5, 6, 7, 8	К5, К8
О8	стены	окраска, Tikkurila, шелковисто-матовая, подготовка Q3	NCS S 1002-Y50R	3	К7
О9	пол	керамогранит, Kerama Marazzi Королевская дорога, 600×1200 мм, SG501600R	Kerama Marazzi SG501600R «Королевская дорога»	4, 5, 6, 7	К10
О10	стены	облицовка плиткой, Italon Charme Extra, 600×1200 мм, 610010001195	Italon 610010001195 «Charme Extra»	6, 7	К11
О11	стены	окраска, Tikkurila, матовая, подготовка Q3	NCS S 0502-Y	8	К12
О12	стены	окраска, Farrow & Ball Modern Emulsion, матовая, подготовка Q3	Farrow & Ball No. 241 «Skimming Stone»	9	К13
О13	акцентная стена	окраска, Farrow & Ball Modern Emulsion, матовая, подготовка Q3	Farrow & Ball No. 30 «Hague Blue»	9	К14
О14	плинтус	плинтус МДФ, Orac Decor Contour (Luxxus), h 69 мм, SX165	Farrow & Ball No. 241 «Skimming Stone»	9	К15

Марки позиций альбома по видам

Префикс	Что обозначает, позиции	Листы
Д	двери: Д-1–Д-4	11–13
ПР	проёмы без полотна (порталы): ПР-1	11–13
ОК	окна: ОК-1–ОК-3	11–13
Г, М, С	мебель и оборудование: Г1, Г2, М1–М11, С1–С8	14–17
П	сантехнические приборы: П1, П3–П6, П20–П22	27–29
ДК	декор (картины, зеркала, растения): ДК3, ДК4	1, 39–43
Т	текстиль (шторы, ковры): Т7–Т12	1, 39–43
Св	светильники: Св5**, Св16–Св25	18–24
Р	розетки: Р9–Р11, Р12**, Р13, Р14	18–24
S	выключатели: S1–S6	18–24
ИП	извещатели: ИП2	18–24

Марки позиций альбома по видам (продолжение)

Префикс	Что обозначает, позиции	Листы
LAN	розетки компьютерные: LAN1, LAN2	18–24
БП	блоки питания LED: БП1, БП2	18–24
ТВ	розетки ТВ: ТВ1, ТВ2	18–24
ЭВ	выводы кабеля: ЭВ2	18–24
ЩК	щиты: ЩК	18–24
ДФ	домофон: ДФ1	18–24
КУП	электроустановочные изделия: КУП1	18–24
Ст В1, Ст К1, Ст Т3	стояки (системы В1, Т3, К1): Ст В1-1, Ст К1-1, Ст Т3-1	27–29
О	марки отделки (реестр альбома): О1–О14	2–4, 53–72
К, КМ	позиции колерной карты: К1–К15, КМ1	36–38
Р	радиаторы отопления: Р-1, Р-2	25, 26

Примечания

1. Марка отделки О — одна на весь альбом: одна и та же отделка (материал, изделие, цвет, формат) на всех листах имеет одну марку; на развёртках и планах стоят марки этого реестра.
2. Столбец «Колер. карта» — позиции колерной карты (лист 36): К — окраска по коду цвета, КМ — материал без кода цвета; «Помещения» — номера по экспликации; количества — по ведомости отделки помещений (лист 35).
3. Марки позиций: один префикс — один вид позиций на весь альбом (двери Д, окна ОК, мебель М, сантехприборы П, декор ДК, текстиль Т, колерная карта К и КМ, радиаторы РО, розетки Р, выключатели S, светильники Св; стояки — «Ст» и система, например «Ст К1-1»). Совпадение префиксов у разных видов — замечание к исходным данным, при выпуске исправляется в модели.

Допущения и предложения на листе


Основа листа: размеры сняты с растрового плана заказчика без размеров: масштаб восстановлен по площадям помещений (≈ 11,8 мм на пиксель), контрольный обмер не выполнен (К-1); высота потолка 2700 мм принята: на плане заказчика её нет (К-2); толщины стен 300 / 120 мм приняты по плану заказчика, не замерены (К-1); разрешённая мощность 15 кВт принята по типовым ТУ для квартиры, ТУ заказчиком не переданы (К-4).
Знак «**» — предложение проектировщика, заказчиком не утверждено (согласовать с заказчиком): записи в реестре нет: Св5 — трековая система 2 × 900 лм: светильник добавлен проектировщиком, поток принят до нормы освещённости, модель и паспорт не выбраны; Р12 — высота 1100 мм выше нормы 1 м (ПУЭ 6.6.30) по назначению: питание ТВ над комодом, в одной зоне с выводами ТВ2 и LAN2.
См. лист открытых вопросов (лист 5, записи К-1, К-2, К-4).

Изм.	Кол.уч	Лист	№ док.	Подп.	Дата	ГД-2026-007-АИ			
						Квартира 65 м²			
						Общая площадь 65,24* м² · * размеры со скана, не замерены (реестр — п. 5, К-1)			
Разраб.		Кырпан А.С.			09.10.26	Дизайн-проект интерьера	Стадия	Лист	Листов
Пров.							РП	53	79
ГИП									
						Реестр марок отделки и позиций альбома	Кырпан Александр Сергеевич		
Н. контр.						М 6/м			
Утв.									

выпуск 09.10.2026 № 147dabfd23 · стр. 64 из 110

Схема расположения развёрток и узлов

План квартиры: марки развёрток по помещениям, выноски узлов, ведомость «марка → лист»

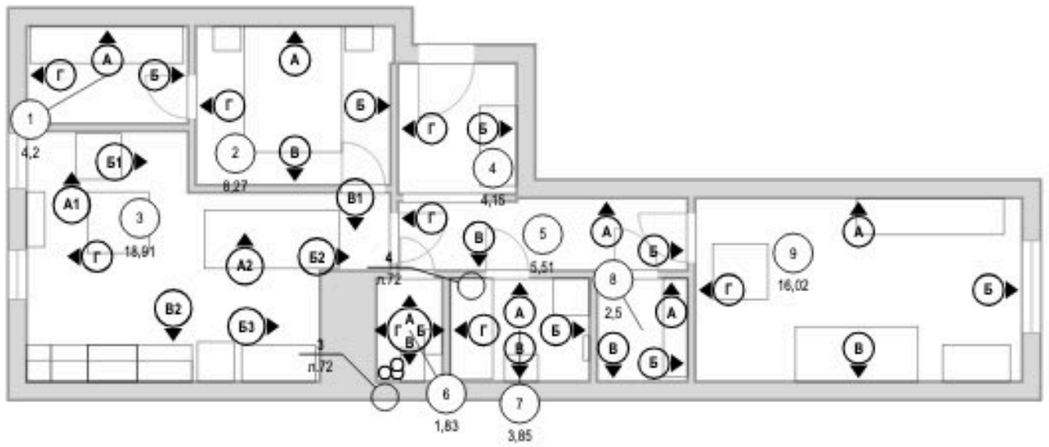

Развёртки и узлы: марка → лист

Марка	Помещение / узел	Лист
А, Б, Г	Гардеробная (пом. 1)	55
А, Б	Спальня (пом. 2)	56
В, Г	Спальня (пом. 2)	57
В2	Кухня-гостиная (пом. 3)	58
Г	Кухня-гостиная (пом. 3)	59
А1, А2, Б1	Кухня-гостиная (пом. 3)	60
Б2, Б3, В1	Кухня-гостиная (пом. 3)	61
Б, Г	Прихожая (пом. 4)	62
А, Б	Коридор (пом. 5)	63
В, Г	Коридор (пом. 5)	64
А, Б	Санузел (пом. 6)	65
В, Г	Санузел (пом. 6)	66
А, Б	Ванная (пом. 7)	67
В, Г	Ванная (пом. 7)	68
А, Б, В	Кладовая (пом. 8)	69
А, Б	Детская (пом. 9)	70
В, Г	Детская (пом. 9)	71
узел 1	Порог 15 мм: мокрая зона — жилое помещение	72
узел 2	Дверь скрытого монтажа в плоскости стены, плинтус	72
узел 3	Короб стояков К1-1 с люком и звукоизоляцией	72
узел 4	Гидроизоляция санузла: заход на стены 200 мм, примыкание ванны	72
узел 5	Плинтус МДФ 69×16 мм у окрашенной стены	72

Условные обозначения

- (А) — марка развёртки: буква стены, стрелка — взгляд
- выноска узла: над полкой — узел, под полкой — лист
- (1) — номер помещения, площадь м²

1000 мм · печать 1:1

Примечания

1. Развёртки — вид на стену изнутри помещения; буквы стен — одна система на весь альбом (как на листах выводов, плитки и отделки).
2. Стены без электроточек, мебели, декора и акцентной отделки развёрток не имеют: их отделка — по ведомости отделки помещений.
3. Узлы — на листе узлов; места применения — по выноскам этого листа и ведомости «марка → лист».

Допущения и предложения на листе

Основа листа: размеры сняты с растрового плана заказчика без размеров: масштаб восстановлен по площадям помещений (≈ 11,8 мм на пиксель), контрольный обмер не выполнен (К-1); высота потолка 2700 мм принята: на плане заказчика её нет (К-2); толщины стен 300 / 120 мм приняты по плану заказчика, не замерены (К-1); разрешённая мощность 15 кВт принята по типовым ТУ для квартиры, ТУ заказчиком не переданы (К-4).
См. лист открытых вопросов (лист 5, записи К-1, К-2, К-4).

Изм.	Кол.уч	Лист	№ док.	Подп.	Дата
Разраб.		Кырпан А.С.			09.10.26
Пров.					
ГИП					
Н. контр.					
Утв.					

ГД-2026-007-АИ

Квартира 65 м²

Общая площадь 65,24* м² · * размеры со скана, не замерены (реестр — п. 5, К-1)

Дизайн-проект интерьера

Стадия	Лист	Листов
РП	54	79

Схема расположения развёрток и узлов

М 1:100

Кырпан Александр Сергеевич


выпуск 09.10.2026 № 147dabfd23 · стр. 65 из 110

Развёртки стен. Гардеробная (пом. 1)


Гардеробная (пом. 1) · вид изнутри помещения · размеры в мм, отметки в м

ПРЕДВАРИТЕЛЬНО · не для производства работ · открыто пунктов: 4 (реестр — л. 5)

Развёртка стены А

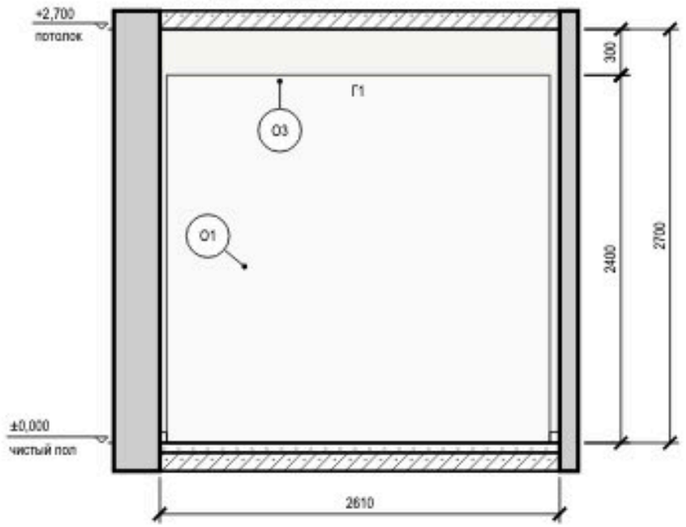

Развёртка стены Б

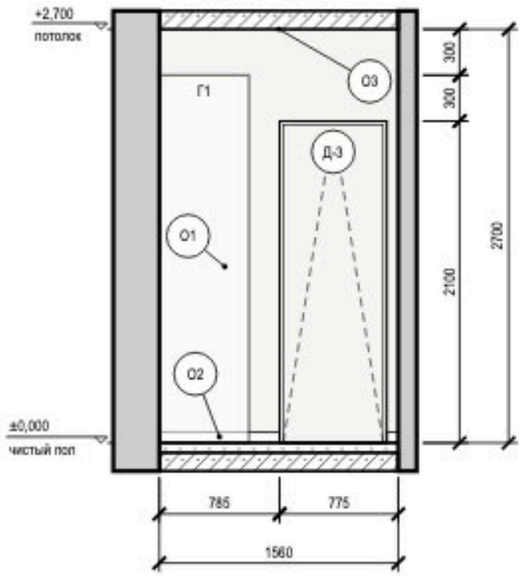

Развёртка стены Г


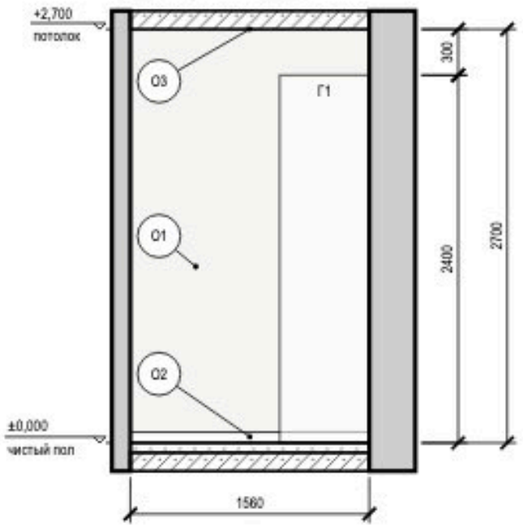


Схема развёрток (М 1:100)

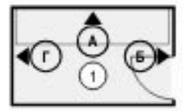

Условные обозначения

- привязки точек и выводов от угла и от пола, мм
- мебель и приборы — фасад по расстановке (условно)
- дверь скрытого монтажа: полотно в плоскости стены (узел — на листе узлов)
- стены и перекрытия в сечении
- окраска: тон — цвет по коду производителя (условно)
- О1 — марка отделки по реестру отделки альбома
- А — марка развёртки: буква стены, стрелка — взгляд

Ведомость отделки (на листе)

Марка	Поверхность	Материал, изделие	Цвет, код	Кол.
О1	стены	окраска, Tikkurila Harmony, матовая, подготовка Q3	Tikkurila V503 «Winter»	14 м²
О2	плинтус	плинтус МДФ, Orac Decor Contour (Luxxus), h 69 мм, SX165	Tikkurila V503 «Winter»	2,5 м
О3	потолок	окраска, Tikkurila Anti-Reflex 2, глубокоматовая, подготовка Q3	Tikkurila V503 «Winter»	4,2 м²

Допущения и предложения на листе

Основа листа: размеры сняты с растрового плана заказчика без размеров: масштаб восстановлен по площадям помещений (≈ 11,8 мм на пиксель), контрольный обмер не выполнен (К-1); высота потолка 2700 мм принята: на плане заказчика её нет (К-2); толщины стен 300 / 120 мм приняты по плану заказчика, не замерены (К-1); разрешённая мощность 15 кВт принята по типовым ТУ для квартиры, ТУ заказчиком не переданы (К-4).
См. лист открытых вопросов (лист 5, записи К-1, К-2, К-4).

Примечания

1. Развёртки — вид на стену изнутри помещения, по часовой стрелке; расположение — на схеме листа и на листе 54; размеры — в мм по чистовым поверхностям; отметки — в м от ±0,000; высоты Н — от чистого пола помещения до оси изделия, у декора — до центра.
2. Красные цепочки — привязки электроточек и выводов: по горизонтали от угла чистовых стен, по вертикали от чистого пола, до оси изделия; звенья короче 3 мм на листе вынесены во второй ярус (ближняя к стене цепочка).
3. У знака электроточки: марка (Р — розетка, S — выключатель, Св — светильник, ЭВ — вывод кабеля), ×N — число постов в рамке, гр. — группа щита, Н — высота оси от чистого пола, мм; группы по клавишам выключателя — на листе выключателей.
4. Схема мебели, приборов и декора не является технической документацией для производства мебели; габариты — по паспортам изделий.
5. Двери скрытого монтажа — полотно в плоскости стены, отделка стены по полотну, плинтус прерывается у короба (узел — на листе узлов).

1000 мм · печать 1:1

Изм.	Кол.уч	Лист	№ док.	Подп.	Дата
Разраб.		Кырпан А.С.			09.10.26
Пров.					
ГИП					
Н. контр.					
Утв.					

ГД-2026-007-АИ

Квартира 65 м²

Общая площадь 65,24* м² · * размеры со скана, не замерены (реестр — п. 5, К-1)

Дизайн-проект интерьера

Стадия	Лист	Листов
РП	55	79

Развёртки стен. Гардеробная (пом. 1)

М 1:40


Кырпан Александр Сергеевич

выпуск 09.10.2026 № 147dabfd23 · стр. 66 из 110

Развёртки стен А, Б. Спальня (пом. 2)

Спальня (пом. 2) · вид изнутри помещения · размеры в мм, отметки в м

Развёртка стены А

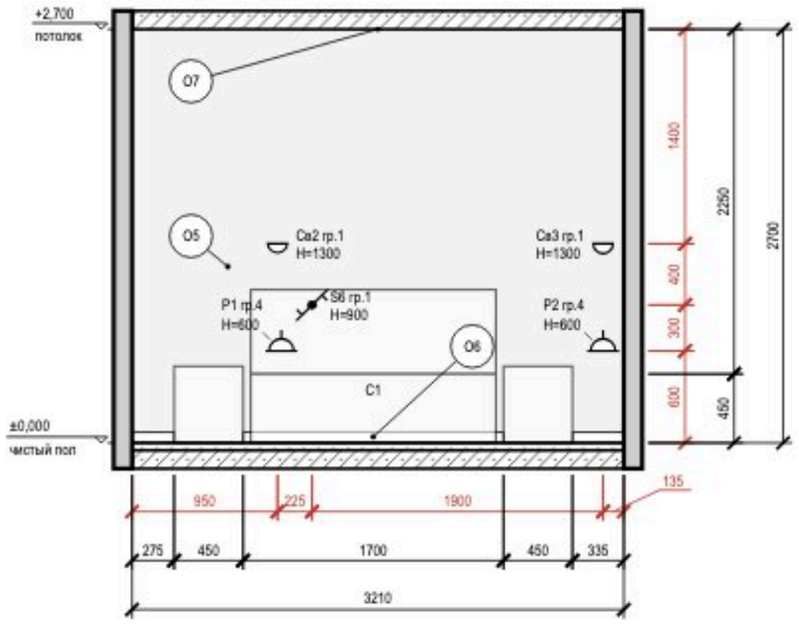

Развёртка стены Б

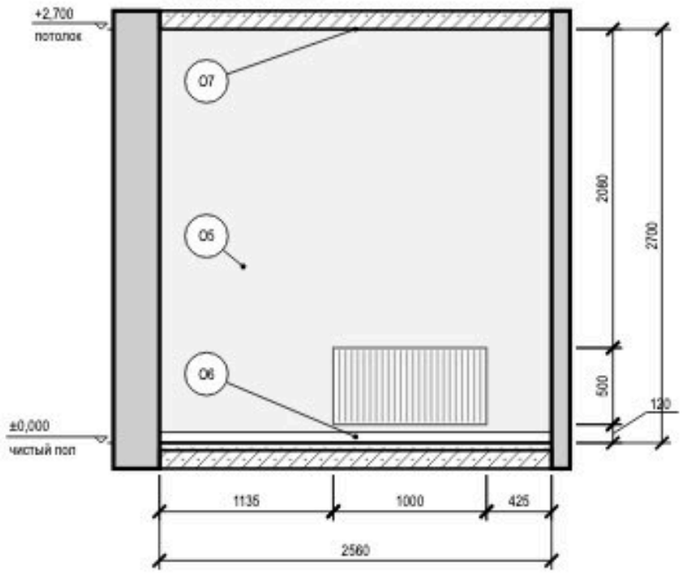


Схема развёрток (М 1:100)



Условные обозначения

- розетка с заземляющим контактом; у знака — марка, ×N постов в рамке, гр. — группа щита, H — высота оси, мм
- выключатель одноклавишный
- выключатель с проходной или перекрёстной клавишей (обратный флажок); тип клавиши — в подписи
- светильник настенный (бра), H — высота оси
- привязки точек и выводов от угла и от пола, мм
- мебель и приборы — фасад по расстановке (условно)
- радиатор отопления; марка — по плану отопления
- стены и перекрытия в сечении
- О1 — марка отделки по реестру отделки альбома
- А — марка развёртки: буква стены, стрелка — взгляд

Ведомость отделки (на листе)

Марка	Поверхность	Материал, изделие	Цвет, код	Кол.
О5	стены	окраска, Tikkurila, глубокоматовая, подготовка Q3	NCS S 1502-Y50R	15,6 м²
О6	плинтус	плинтус МДФ, Orac Decor Contour (Luxxus), h 69 мм, SX165, шелковисто-матовая	NCS S 0300-N	4,9 м
О7	потолок	окраска, Tikkurila, глубокоматовая	NCS S 0300-N	8,3 м²

Допущения и предложения на листе

Основа листа: размеры сняты с растрового плана заказчика без размеров: масштаб восстановлен по площадям помещений (≈ 11,8 мм на пиксель), контрольный обмер не выполнен (К-1); высота потолка 2700 мм принята: на плане заказчика её нет (К-2); толщины стен 300 / 120 мм приняты по плану заказчика, не замерены (К-1); разрешённая мощность 15 кВт принята по типовым ТУ для квартиры, ТУ заказчиком не переданы (К-4).

См. лист открытых вопросов (лист 5, записи К-1, К-2, К-4).

Примечания

1. Развёртки — вид на стену изнутри помещения, по часовой стрелке; расположение — на схеме листа и на листе 54; размеры — в мм по чистовым поверхностям; отметки — в м от ±0,000; высоты H — от чистого пола помещения до оси изделия, у декора — до центра.
2. Красные цепочки — привязки электроточек и выводов: по горизонтали от угла чистовых стен, по вертикали от чистого пола, до оси изделия; звенья короче 3 мм на листе вынесены во второй ярус (ближняя к стене цепочка).
3. У знака электроточки: марка (Р — розетка, S — выключатель, Св — светильник, ЭВ — вывод кабеля), ×N — число постов в рамке, гр. — группа щита, H — высота оси от чистого пола, мм; группы по клавишам выключателя — на листе выключателей.
4. Схема мебели, приборов и декора не является технической документацией для производства мебели; габариты — по паспортам изделий.

1000 мм · печать 1:1

Изм.	Кол.уч	Лист	№ док.	Подп.	Дата
Разраб.		Кырпан А.С.			09.10.26
Пров.					
ГИП					
Н. контр.					
Утв.					

ГД-2026-007-АИ

Квартира 65 м²

Общая площадь 65,24* м² · * размеры со скана, не замерены (реестр — п. 5, К-1)

Дизайн-проект интерьера

Стадия	Лист	Листов
РП	56	79

Развёртки стен А, Б. Спальня (пом. 2)

М 1:40

Кырпан Александр Сергеевич


выпуск 09.10.2026 · 147dabfd23 · стр. 67 из 110

Развёртки стен В, Г. Спальня (пом. 2)

Спальня (пом. 2) · вид изнутри помещения · размеры в мм, отметки в м

ПРЕДВАРИТЕЛЬНО · не для производства работ · открыто пунктов: 4 (реестр — л. 5)

Развёртка стены В

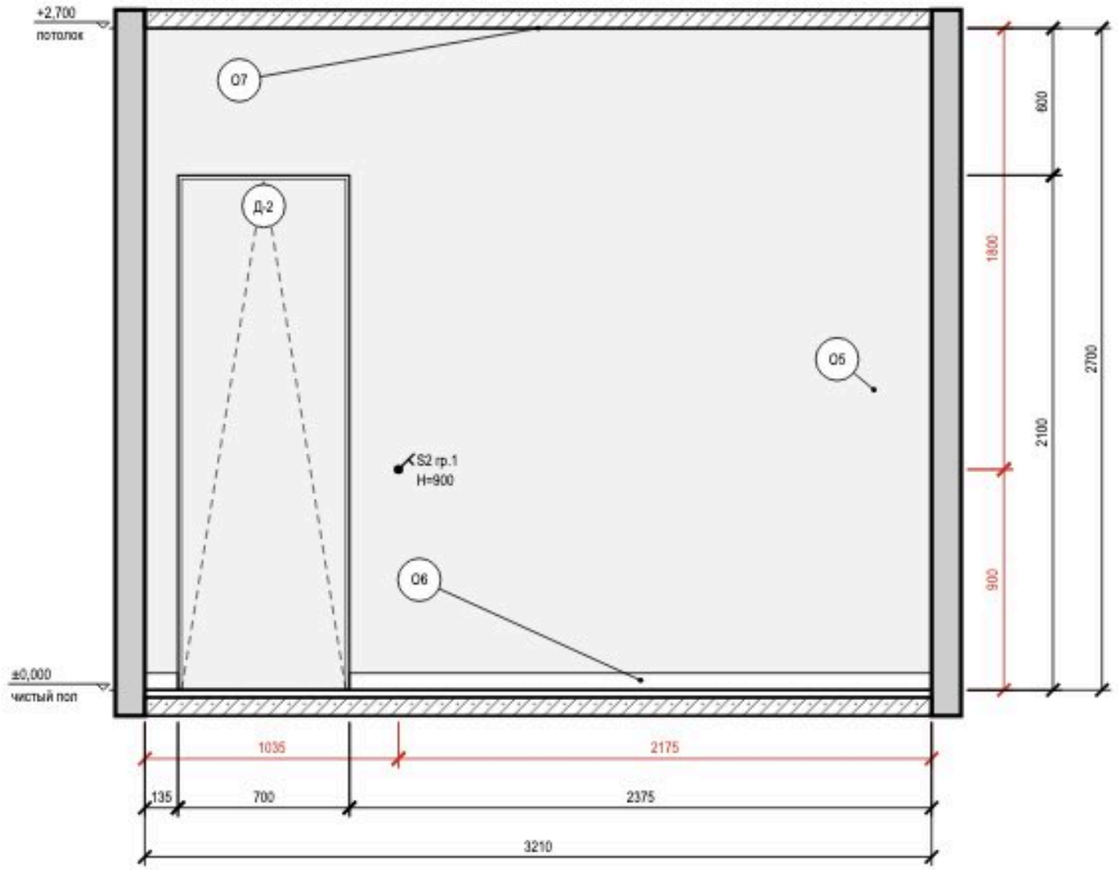

Развёртка стены Г

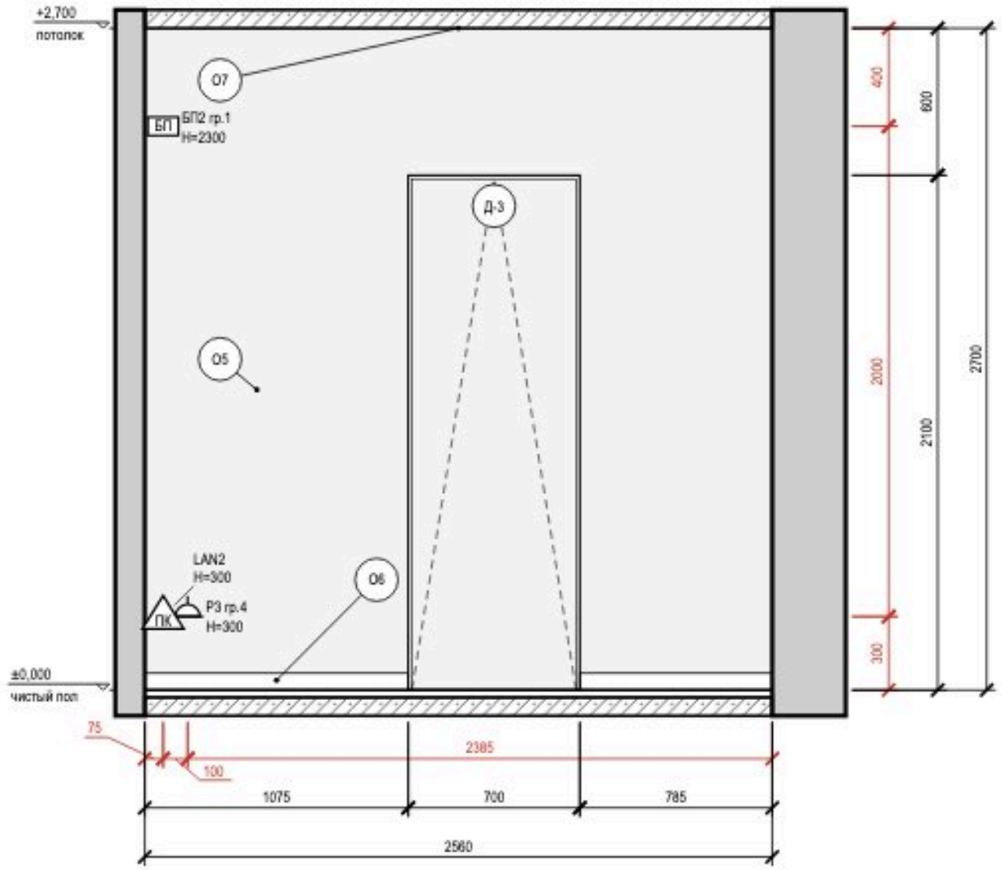


Схема развёрток (М 1:100)



Условные обозначения

- розетка с заземляющим контактом; у знака — марка, ×N постов в рамке, гр. — группа щита, H — высота оси, мм
- выключатель одноклавишный
- БП — блок питания LED, с доступом (люк от 100×100 мм)
- ПК — розетка компьютерная RJ45
- привязки точек и выводов от угла и от пола, мм
- мебель и приборы — фасад по расстановке (условно)
- дверь скрытого монтажа: полотно в плоскости стены (узел — на листе узлов)
- стены и перекрытия в сечении
- О1 — марка отделки по реестру отделки альбома
- А — марка развёртки: буква стены, стрелка — взгляд

Ведомость отделки (на листе)

Марка	Поверхность	Материал, изделие	Цвет, код	Кол.
О5	стены	окраска, Tikkurila, глубокоматовая, подготовка Q3	NCS S 1502-Y50R	12,6 м²
О6	плинтус	плинтус МДФ, Orac Decor Contour (Luxxus), h 69 мм, SX165, шелковисто-матовая	NCS S 0300-N	4,4 м
О7	потолок	окраска, Tikkurila, глубокоматовая	NCS S 0300-N	8,3 м²

Допущения и предложения на листе

Основа листа: размеры сняты с растрового плана заказчика без размеров; масштаб восстановлен по площадям помещений (≈ 11,8 мм на пиксель), контрольный обмер не выполнен (К-1); высота потолка 2700 мм принята: на плане заказчика её нет (К-2); толщины стен 300 / 120 мм приняты по плану заказчика, не замерены (К-1); разрешённая мощность 15 кВт принята по типовым ТУ для квартиры, ТУ заказчиком не переданы (К-4).

Примечания

См. лист открытых вопросов (лист 5, записи К-1, К-2, К-4).

1. Развёртки — вид на стену изнутри помещения, по часовой стрелке; расположение — на схеме листа и на листе 54; размеры — в мм по чистовым поверхностям; отметки — в м от ±0,000; высоты H — от чистого пола помещения до оси изделия, у декора — до центра.
2. Красные цепочки — привязки электроточек и выводов: по горизонтали от угла чистовых стен, по вертикали от чистого пола, до оси изделия; звенья короче 3 мм на листе вынесены во второй ярус (ближние к стене цепочка).
3. У знака электроточки: марка (Р — розетка, S — выключатель, Св — светильник, ЭВ — вывод кабеля), ×N — число постов в рамке, гр. — группа щита, H — высота оси от чистого пола, мм; группы по клавишам выключателя — на листе выключателей.
4. Схема мебели, приборов и декора не является технической документацией для производства мебели; габариты — по паспортам изделий.
5. Двери скрытого монтажа — полотно в плоскости стены, отделка стены по полотну, плинтус прерывается у короба (узел — на листе узлов).

1000 мм · печать 1:1

Изм.	Кол.уч	Лист	№ док.	Подп.	Дата
Разраб.		Кырпан А.С.			09.10.26
Пров.					
ГИП					
Н. контр.					
Утв.					

ГД-2026-007-АИ

Квартира 65 м²

Общая площадь 65,24* м² · * размеры со скана, не замерены (реестр — п. 5, К-1)

Дизайн-проект интерьера	Стадия	Лист	Листов
	РП	57	79

Развёртки стен В, Г. Спальня (пом. 2)

М 1:25

Кырпан Александр Сергеевич

выпуск 09.10.2026 № 147dabfd23 · стр. 68 из 110

Развёртка стены В2. Кухня-гостиная (пом. 3), кухонный фронт

Кухня-гостиная (пом. 3) · вид изнутри помещения · размеры в мм, отметки в м

ПРЕДВАРИТЕЛЬНО · не для производства работ · открыто пунктов: 4 (реестр — л. 5)

Развёртка стены В2

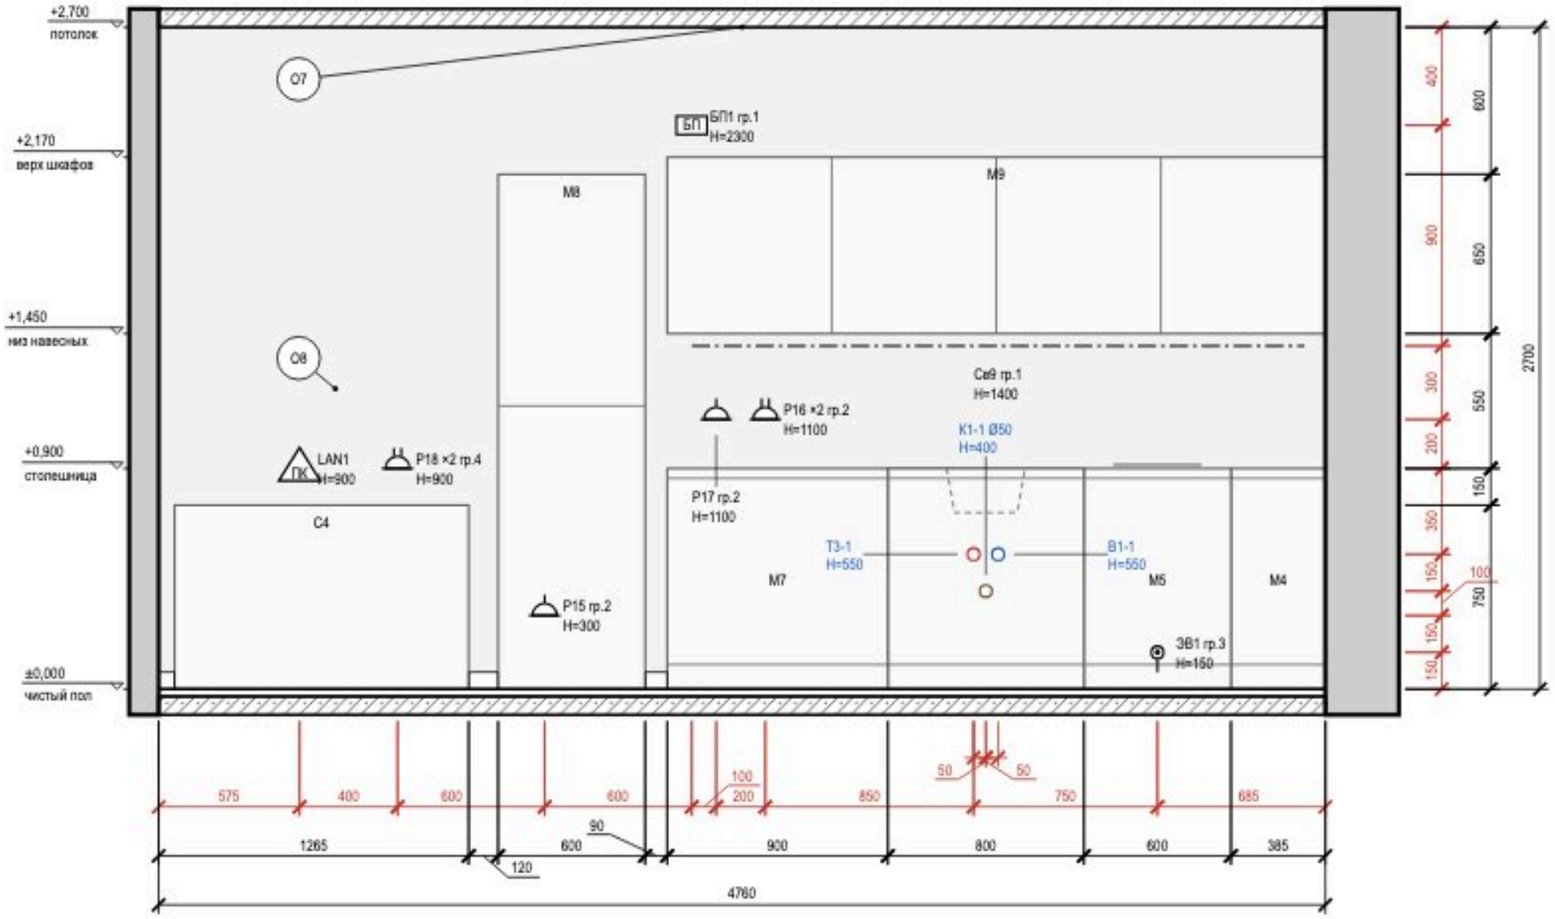


Схема развёрток (М 1:100)



Условные обозначения

- розетка с заземляющим контактом; у знака — марка, ×N постов в рамке, гр. — группа щита, H — высота оси, мм
- вывод кабеля для подключения прибора (без розетки), марка ЭВ
- светодиодная лента в профиле / в карнизе короба
- БП — блок питания LED, с доступом (люк от 100×100 мм)
- ПК — розетка компьютерная RJ45
- вывод В1 (код — в ведомости привязок)
- вывод Т3 (код — в ведомости привязок)
- вывод К1 (код — в ведомости привязок)
- привязки точек и выводов от угла и от пола, мм
- мебель и приборы — фасад по расстановке (условно)
- стены и перекрытия в сечении
- О1 — марка отделки по реестру отделки альбома
- А — марка развёртки: буква стены, стрелка — взгляд

Ведомость отделки (на листе)

Марка	Поверхность	Материал, изделие	Цвет, код	Кол.
О6	плинтус	плинтус МДФ, Orac Decor Contour (Luxxus), h 69 мм, SX165, шелковисто-матовая	NCS S 0300-N	0,3 м
О7	потолок	окраска, Tikkurila, глубокоматовая	NCS S 0300-N	18,9 м²
О8	стены	окраска, Tikkurila, шелковисто-матовая, подготовка Q3	NCS S 1002-Y50R	12,9 м²

Допущения и предложения на листе

Основа листа: размеры сняты с растрового плана заказчика без размеров: масштаб восстановлен по площадям помещений (≈ 11,8 мм на пиксель), контрольный обмер не выполнен (К-1); высота потолка 2700 мм принята: на плане заказчика её нет (К-2); толщины стен 300 / 120 мм приняты по плану заказчика, не замерены (К-1); разрешённая мощность 15 кВт принята по типовым ТУ для квартиры, ТУ заказчиком не переданы (К-4).
См. лист открытых вопросов (лист 5, записи К-1, К-2, К-4).

Примечания

1. Развёртки — вид на стену изнутри помещения, по часовой стрелке; расположение — на схеме листа и на листе 54; размеры — в мм по чистовым поверхностям; отметки — в м от ±0,000; высоты H — от чистого пола помещения до оси изделия, у декора — до центра.
2. Красные цепочки — привязки электроточек и выводов: по горизонтали от угла чистовых стен, по вертикали от чистого пола, до оси изделия; звенья короче 3 мм на листе вынесены во второй ярус (ближняя к стене цепочка).
3. У знака электроточки: марка (Р — розетка, S — выключатель, Св — светильник, ЭВ — вывод кабеля), ×N — число постов в рамке, гр. — группа щита, H — высота оси от чистого пола, мм; группы по клавишам выключателя — на листе выключателей.
4. Схема мебели, приборов и декора не является технической документацией для производства мебели; габариты — по паспортам изделий.
5. Выводы кухонной техники — по утверждённому проекту кухни: привязки выводов даются от осей модулей гарнитура.

1000 мм · печать 1:1

Изм.	Кол.уч	Лист	№ док.	Подп.	Дата
Разраб.		Кырпан А.С.			09.10.26
Пров.					
ГИП					
Н. контр.					
Утв.					

ГД-2026-007-АИ

Квартира 65 м²

Общая площадь 65,24* м² · * размеры со скана, не замерены (реестр — п. 5, К-1)

Дизайн-проект интерьера

Стадия	Лист	Листов
РП	58	79

Развёртка стены В2. Кухня-гостиная (пом. 3), кухонный фронт

М 1:25

Кырпан Александр Сергеевич

выпуск 09.10.2026 · 147dabfd23 · стр. 69 из 110

Развёртка стены Г. Кухня-гостиная (пом. 3), кухонный фронт

Кухня-гостиная (пом. 3) · вид изнутри помещения · размеры в мм, отметки в м

ПРЕДВАРИТЕЛЬНО · не для производства работ · открыто пунктов: 4 (реестр — л. 5)

Развёртка стены Г

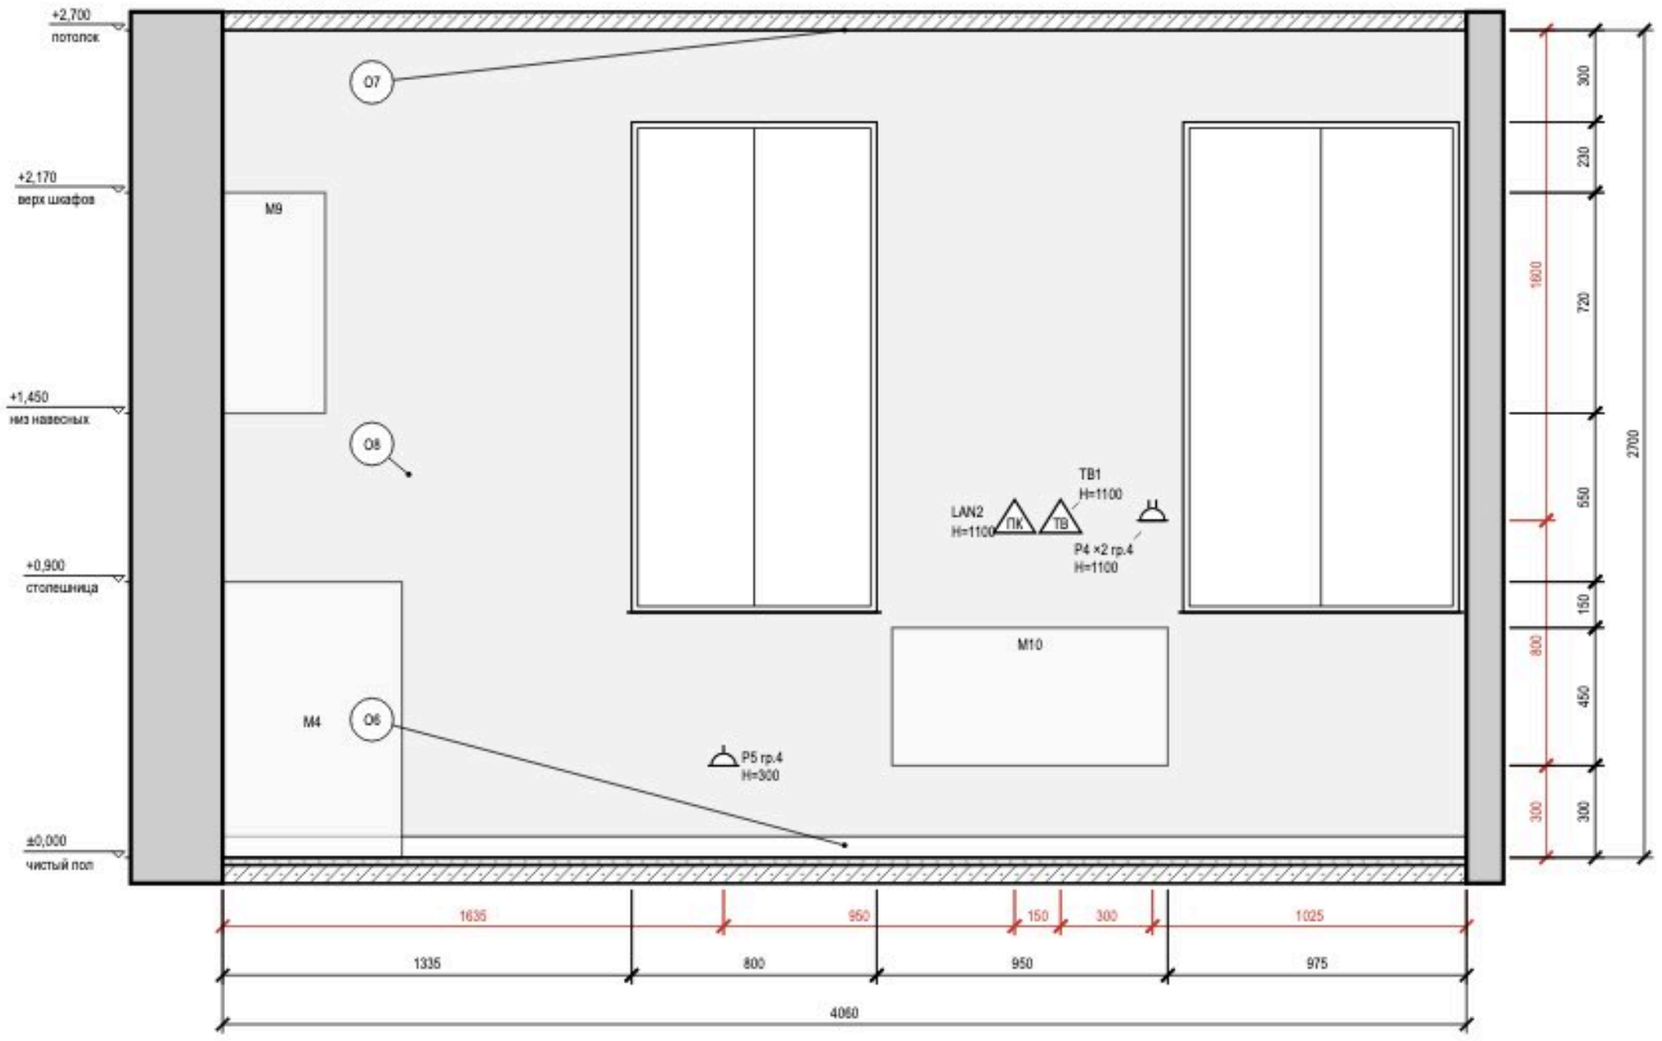


Схема развёрток (М 1:100)



Условные обозначения

- розетка с заземляющим контактом; у знака — марка, ×N постов в рамке, гр. — группа щита, H — высота оси, мм
- ПК — розетка компьютерная RJ45
- ТВ — розетка телевизионная
- привязки точек и выводов от угла и от пола, мм
- мебель и приборы — фасад по расстановке (условно)
- окно: проём, рама, подоконник
- стены и перекрытия в сечении
- О1 — марка отделки по реестру отделки альбома
- А — марка развёртки: буква стены, стрелка — взгляд

Допущения и предложения на листе

Основа листа: размеры сняты с растрового плана заказчика без размеров: масштаб восстановлен по площадям помещений (≈ 11,8 мм на пиксель), контрольный обмер не выполнен (К-1); высота потолка 2700 мм принята: на плане заказчика её нет (К-2); толщины стен 300 / 120 мм приняты по плану заказчика, не замерены (К-1); разрешённая мощность 15 кВт принята по типовым ТУ для квартиры, ТУ заказчиком не переданы (К-4).

См. лист открытых вопросов (лист 5, записи К-1, К-2, К-4).

Примечания

1. Развёртки — вид на стену изнутри помещения, по часовой стрелке; расположение — на схеме листа и на листе 54; размеры — в мм по чистовым поверхностям; отметки — в м от ±0,000; высоты H — от чистого пола помещения до оси изделия, у декора — до центра.
2. Красные цепочки — привязки электроточек и выводов: по горизонтали от угла чистовых стен, по вертикали от чистого пола, до оси изделия; звенья короче 3 мм на листе вынесены во второй ярус (ближняя к стене цепочка).
3. У знака электроточки: марка (Р — розетка, S — выключатель, Св — светильник, ЭВ — вывод кабеля), ×N — число постов в рамке, гр. — группа щита, H — высота оси от чистого пола, мм; группы по клавишам выключателя — на листе выключателей.
4. Схема мебели, приборов и декора не является технической документацией для производства мебели; габариты — по паспортам изделий.
5. Выводы кухонной техники — по утверждённому проекту кухни: привязки выводов даются от осей модулей гарнитура.

1000 мм · печать 1:1

Изм.	Кол.уч	Лист	№ док.	Подп.	Дата
Разраб.		Кырпан А.С.			09.10.26
Пров.					
ГИП					
Н. контр.					
Утв.					

ГД-2026-007-АИ

Квартира 65 м²

Общая площадь 65,24* м² · * размеры со скана, не замерены (реестр — п. 5, К-1)

Дизайн-проект интерьера	Стадия	Лист	Листов
	РП	59	79

Развёртка стены Г. Кухня-гостиная (пом. 3), кухонный фронт

М 1:20

Кырпан Александр Сергеевич


выпуск 09.10.2026 № 147dabfd23 · стр. 70 из 110

Развёртки стен А1, А2, Б1. Кухня-гостиная (пом. 3)


Кухня-гостиная (пом. 3) · вид изнутри помещения · размеры в мм, отметки в м

ПРЕДВАРИТЕЛЬНО · не для производства работ · открыто пунктов: 4 (реестр — л. 5)

Развёртка стены А1

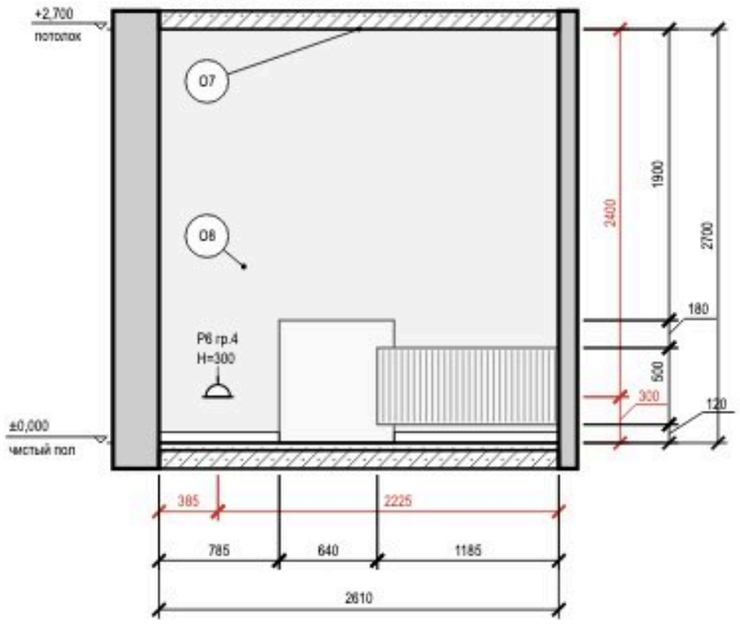

Развёртка стены А2

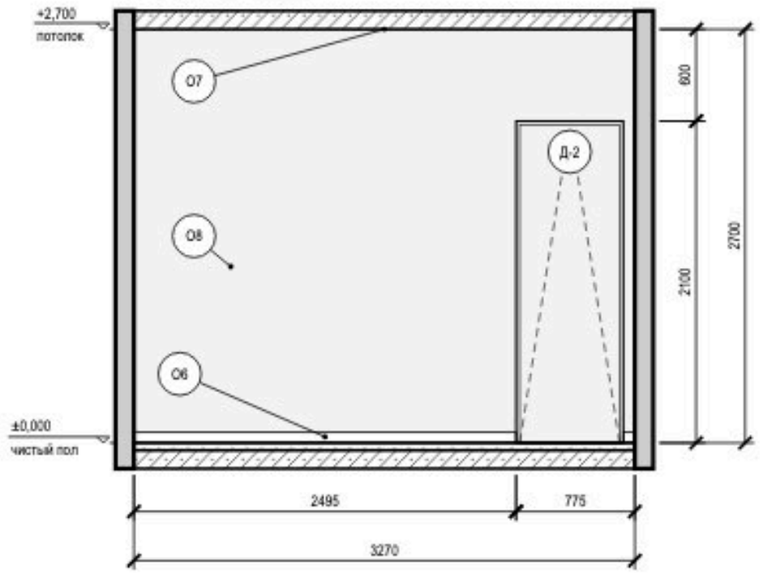

Развёртка стены Б1

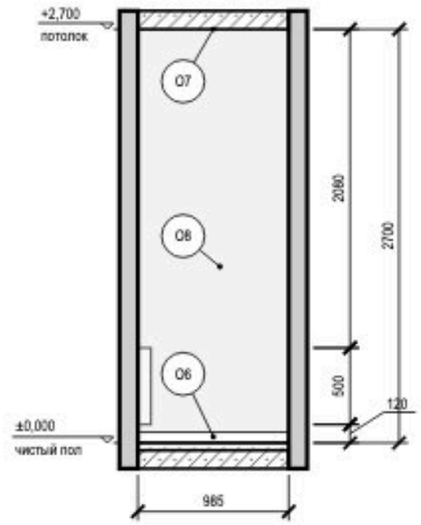


Схема развёрток (М 1:100)



Условные обозначения

- розетка с заземляющим контактом; у знака — марка, ×N постов в рамке, гр. — группа щита, Н — высота оси, мм
- привязки точек и выводов от угла и от пола, мм
- мебель и приборы — фасад по расстановке (условно)
- дверь скрытого монтажа: полотно в плоскости стены (узел — на листе узлов)
- радиатор отопления; марка — по плану отопления
- стены и перекрытия в сечении
- О1 — марка отделки по реестру отделки альбома
- А — марка развёртки: буква стены, стрелка — взгляд

Ведомость отделки (на листе)

Марка	Поверхность	Материал, изделие	Цвет, код	Кол.
О6	плинтус	плинтус МДФ, Orac Decor Contour (Luxxus), h 69 мм, SX165, шелковисто-матовая	NCS S 0300-N	5,4 м
О7	потолок	окраска, Tikkurila, глубокоматовая	NCS S 0300-N	18,9 м²
О8	стены	окраска, Tikkurila, шелковисто-матовая, подготовка Q3	NCS S 1002-Y50R	17,1 м²

Допущения и предложения на листе

Основа листа: размеры сняты с растрового плана заказчика без размеров: масштаб восстановлен по площадям помещений (≈ 11,8 мм на пиксель), контрольный обмер не выполнен (К-1); высота потолка 2700 мм принята: на плане заказчика её нет (К-2); толщины стен 300 / 120 мм приняты по плану заказчика, не замерены (К-1); разрешённая мощность 15 кВт принята по типовым ТУ для квартиры, ТУ заказчиком не переданы (К-4).

См. лист открытых вопросов (лист 5, записи К-1, К-2, К-4).

Примечания

1. Развёртки — вид на стену изнутри помещения, по часовой стрелке; расположение — на схеме листа и на листе 54; размеры — в мм по чистовым поверхностям; отметки — в м от ±0,000; высоты Н — от чистого пола помещения до оси изделия, у декора — до центра.
2. Красные цепочки — привязки электроточек и выводов: по горизонтали от угла чистовых стен, по вертикали от чистого пола, до оси изделия; звенья короче 3 мм на листе вынесены во второй ярус (ближняя к стене цепочка).
3. У знака электроточки: марка (Р — розетка, S — выключатель, Св — светильник, ЭВ — вывод кабеля), ×N — число постов в рамке, гр. — группа щита, Н — высота оси от чистого пола, мм; группы по клавишам выключателя — на листе выключателей.
4. Схема мебели, приборов и декора не является технической документацией для производства мебели; габариты — по паспортам изделий.
5. Двери скрытого монтажа — полотно в плоскости стены, отделка стены по полотну, плинтус прерывается у короба (узел — на листе узлов).

1000 мм · печать 1:1

Изм.	Кол.уч	Лист	№ док.	Подп.	Дата
Разраб.		Кырпан А.С.			09.10.26
Пров.					
ГИП					
Н. контр.					
Утв.					

ГД-2026-007-АИ

Квартира 65 м²

Общая площадь 65,24* м² · * размеры со скана, не замерены (реестр — п. 5, К-1)

Дизайн-проект интерьера

Стадия	Лист	Листов
РП	60	79

Развёртки стен А1, А2, Б1. Кухня-гостиная (пом. 3)

М 1:40


Кырпан Александр Сергеевич

выпуск 09.10.2026 · 147dabfd23 · стр. 71 из 110


Развёртки стен Б2, Б3, В1. Кухня-гостиная (пом. 3)

Кухня-гостиная (пом. 3) · вид изнутри помещения · размеры в мм, отметки в м

Развёртка стены Б2

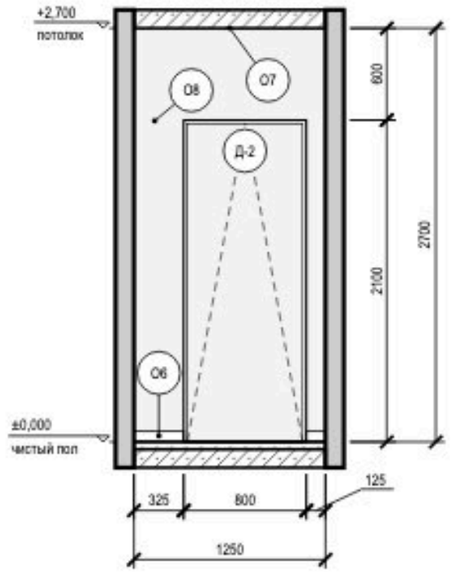

Развёртка стены Б3

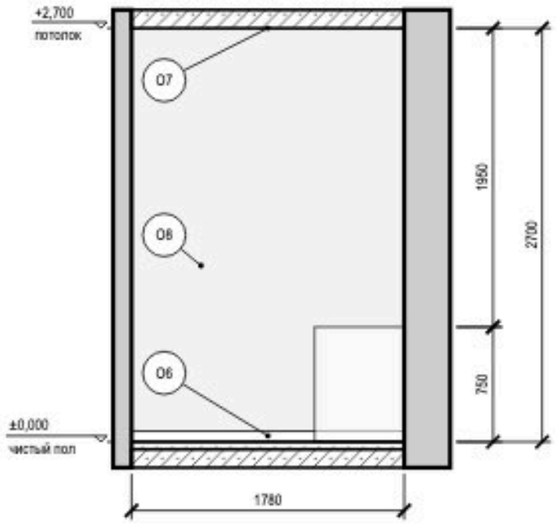

Развёртка стены В1


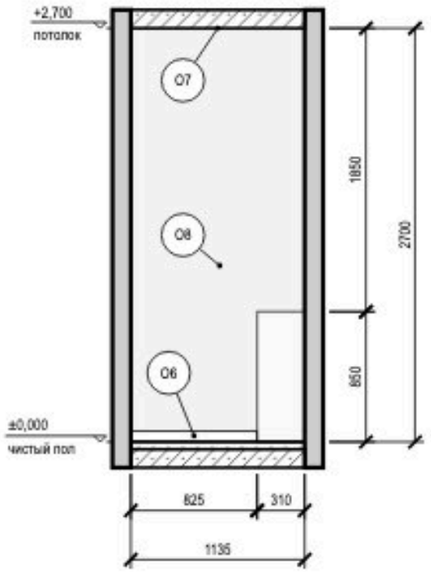


Схема развёрток (М 1:100)

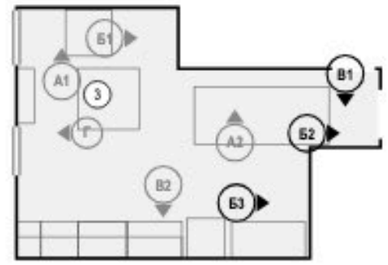

Условные обозначения

- привязки точек и выводов от угла и от пола, мм
- мебель и приборы — фасад по расстановке (условно)
- дверь скрытого монтажа: полотно в плоскости стены (узел — на листе узлов)
- стены и перекрытия в сечении
- О1 — марка отделки по реестру отделки альбома
- А — марка развёртки: буква стены, стрелка — взгляд

Ведомость отделки (на листе)

Марка	Поверхность	Материал, изделие	Цвет, код	Кол.
О6	плинтус	плинтус МДФ, Orac Decor Contour (Luxxus), h 69 мм, SX165, шелковисто-матовая	NCS S 0300-N	3,1 м
О7	потолок	окраска, Tikkurila, глубокоматовая	NCS S 0300-N	18,9 м²
О8	стены	окраска, Tikkurila, шелковисто-матовая, подготовка Q3	NCS S 1002-Y50R	9,6 м²

Допущения и предложения на листе

Основа листа: размеры сняты с растрового плана заказчика без размеров: масштаб восстановлен по площадям помещений (≈ 11,8 мм на пиксель), контрольный обмер не выполнен (К-1); высота потолка 2700 мм принята: на плане заказчика её нет (К-2); толщины стен 300 / 120 мм приняты по плану заказчика, не замерены (К-1); разрешённая мощность 15 кВт принята по типовым ТУ для квартиры, ТУ заказчиком не переданы (К-4).

См. лист открытых вопросов (лист 5, записи К-1, К-2, К-4).

Примечания

1. Развёртки — вид на стену изнутри помещения, по часовой стрелке; расположение — на схеме листа и на листе 54; размеры — в мм по чистовым поверхностям; отметки — в м от ±0,000; высоты Н — от чистого пола помещения до оси изделия, у декора — до центра.
2. Красные цепочки — привязки электроточек и выводов: по горизонтали от угла чистовых стен, по вертикали от чистого пола, до оси изделия; звенья короче 3 мм на листе вынесены во второй ярус (ближняя к стене цепочка).
3. У знака электроточки: марка (Р — розетка, S — выключатель, Св — светильник, ЭВ — вывод кабеля), ×N — число постов в рамке, гр. — группа щита, Н — высота оси от чистого пола, мм; группы по клавишам выключателя — на листе выключателей.
4. Схема мебели, приборов и декора не является технической документацией для производства мебели; габариты — по паспортам изделий.
5. Двери скрытого монтажа — полотно в плоскости стены, отделка стены по полотну, плинтус прерывается у короба (узел — на листе узлов).

1000 мм · печать 1:1

Изм.	Кол.уч	Лист	№ док.	Подп.	Дата
Разраб.		Кырпан А.С.			09.10.26
Пров.					
ГИП					
Н. контр.					
Утв.					

ГД-2026-007-АИ

Квартира 65 м²

Общая площадь 65,24* м² · * размеры со скана, не замерены (реестр — п. 5, К-1)

Дизайн-проект интерьера	Стадия	Лист	Листов
	РП	61	79

Развёртки стен Б2, Б3, В1. Кухня-гостиная (пом. 3)

М 1:40

Кырпан Александр Сергеевич


выпуск 09.10.2026 № 147dabfd23 · стр. 72 из 110

Развёртки стен. Прихожая (пом. 4)


Прихожая (пом. 4) · вид изнутри помещения · размеры в мм, отметки в м

ПРЕДВАРИТЕЛЬНО · не для производства работ · открыто пунктов: 4 (реестр — л. 5)

Развёртка стены Б

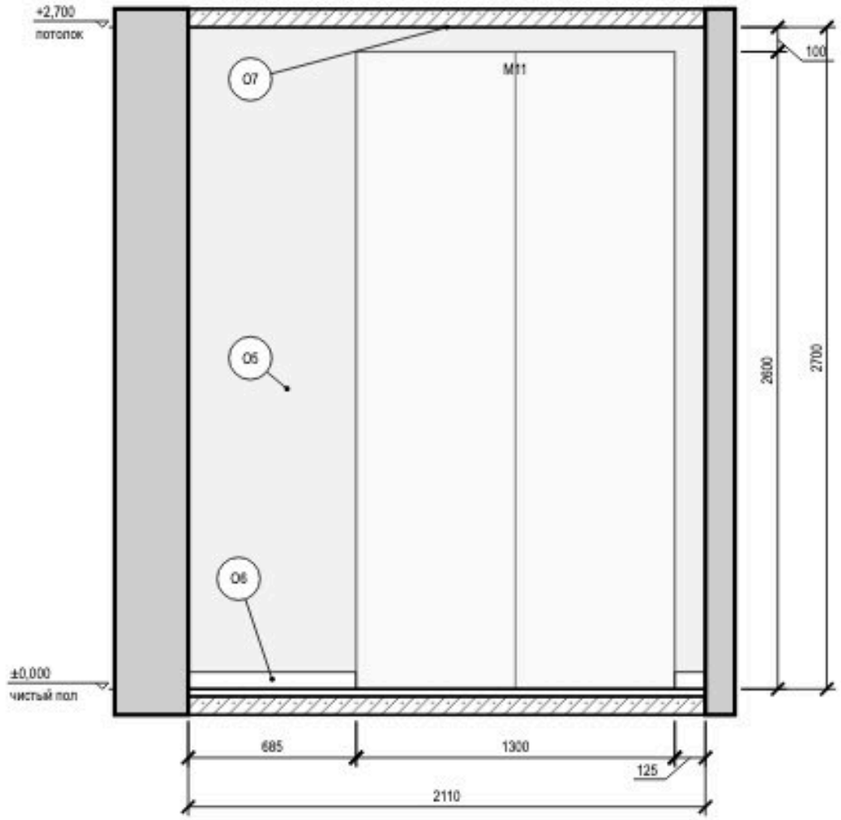


Развёртка стены Г

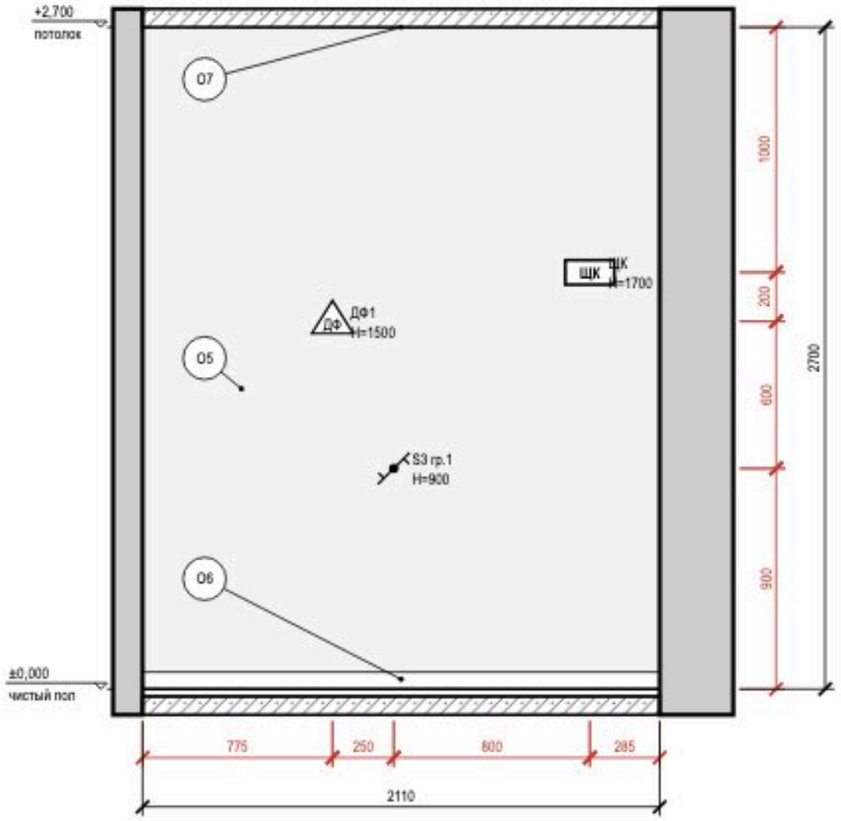

Условные обозначения

- выключатель одноклавишный
- выключатель с проходной или перекрёстной клавишей (обратный флажок); тип клавиши — в подписи
- ДФ — трубка или монитор домофона
- ЩК — щит квартирный
- привязки точек и выводов от угла и от пола, мм
- мебель и приборы — фасад по расстановке (условно)
- стены и перекрытия в сечении
- О1 — марка отделки по реестру отделки альбома
- А — марка развёртки: буква стены, стрелка — взгляд

Схема развёрток (М 1:100)

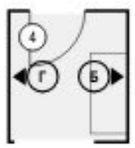

Ведомость отделки (на листе)

Марка	Поверхность	Материал, изделие	Цвет, код	Кол.
О5	стены	окраска, Tikkurila, шелковисто-матовая, подготовка Q3	NCS S 1502-Y50R	11,4 м²
О6	плинтус	плинтус МДФ, Orac Decor Contour (Luxxus), h 69 мм, SX165, шелковисто-матовая	NCS S 0300-N	2,9 м
О7	потолок	окраска, Tikkurila, глубокоматовая	NCS S 0300-N	4,2 м²

Допущения и предложения на листе

Основа листа: размеры сняты с растрового плана заказчика без размеров: масштаб восстановлен по площадям помещений (≈ 11,8 мм на пиксель), контрольный обмер не выполнен (К-1); высота потолка 2700 мм принята: на плане заказчика её нет (К-2); толщины стен 300 / 120 мм приняты по плану заказчика, не замерены (К-1); разрешённая мощность 15 кВт принята по типовым ТУ для квартиры, ТУ заказчиком не переданы (К-4).

См. лист открытых вопросов (лист 5, записи К-1, К-2, К-4).

Примечания

1. Развёртки — вид на стену изнутри помещения, по часовой стрелке; расположение — на схеме листа и на листе 54; размеры — в мм по чистовым поверхностям; отметки — в м от ±0,000; высоты Н — от чистого пола помещения до оси изделия, у декора — до центра.
2. Красные цепочки — привязки электроточек и выводов: по горизонтали от угла чистовых стен, по вертикали от чистого пола, до оси изделия; звенья короче 3 мм на листе вынесены во второй ярус (ближние к стене цепочка).
3. У знака электроточки: марка (Р — розетка, S — выключатель, Св — светильник, ЭВ — вывод кабеля), ×N — число постов в рамке, гр. — группа щита, Н — высота оси от чистого пола, мм; группы по клавишам выключателя — на листе выключателей.
4. Схема мебели, приборов и декора не является технической документацией для производства мебели; габариты — по паспортам изделий.

1000 мм · печать 1:1

Изм.	Кол.уч	Лист	№ док.	Подп.	Дата
Разраб.		Кырпан А.С.			09.10.26
Пров.					
ГИП					
Н. контр.					
Утв.					

ГД-2026-007-АИ

Квартира 65 м²

Общая площадь 65,24* м² · * размеры со скана, не замерены (реестр — п. 5, К-1)

Дизайн-проект интерьера

Стадия	Лист	Листов
РП	62	79

Развёртки стен. Прихожая (пом. 4)

М 1:25

Кырпан Александр Сергеевич


выпуск 09.10.2026 · 147dabfd23 · стр. 73 из 110

Развёртки стен А, Б. Коридор (пом. 5)

Коридор (пом. 5) · вид изнутри помещения · размеры в мм, отметки в м

ПРЕДВАРИТЕЛЬНО · не для производства работ · открыто пунктов: 4 (реестр — л. 5)

Развёртка стены А

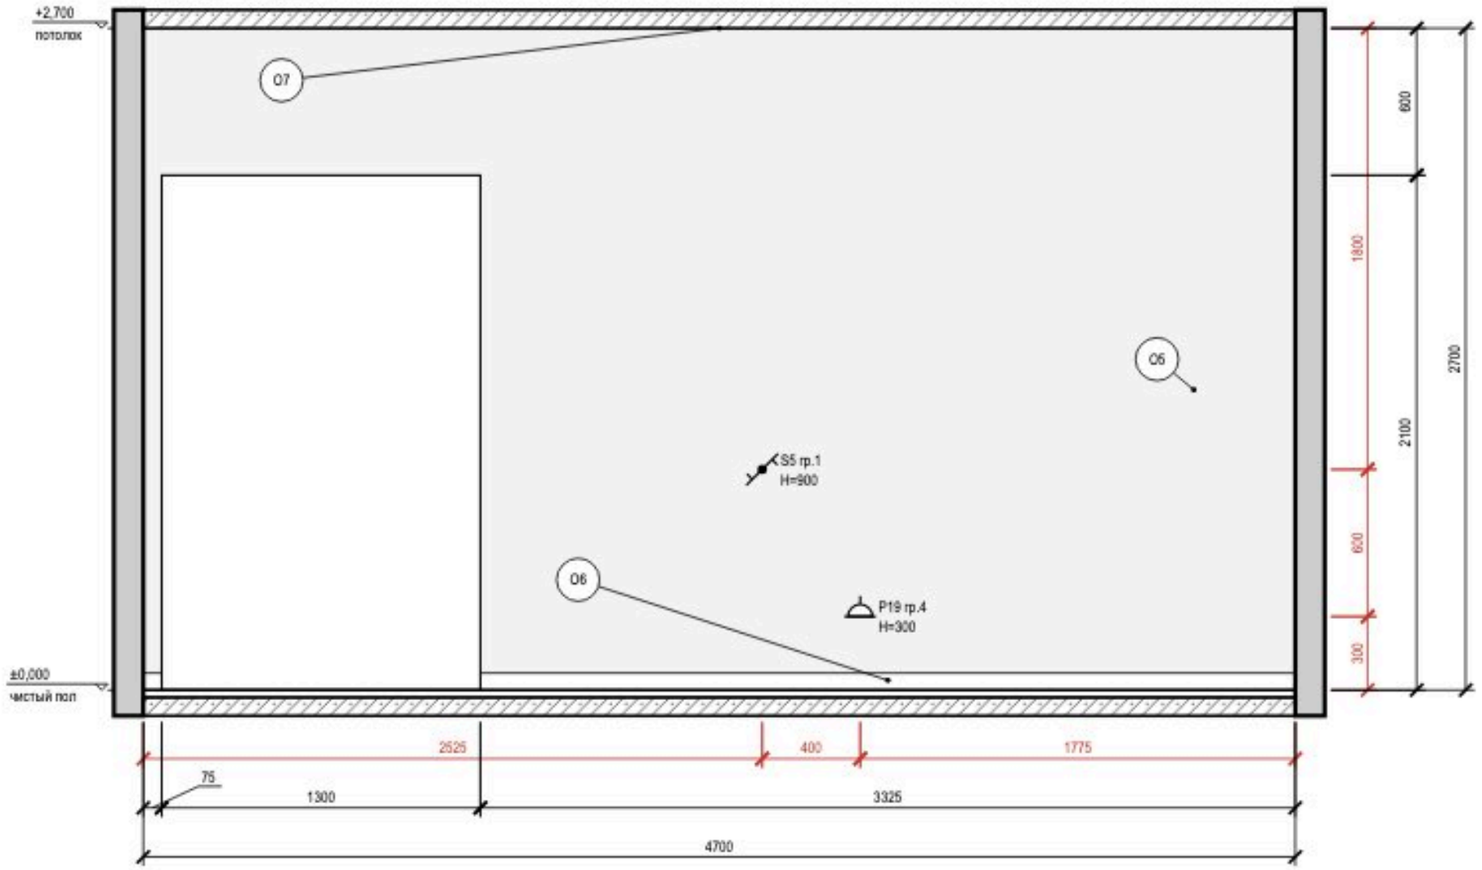

Развёртка стены Б

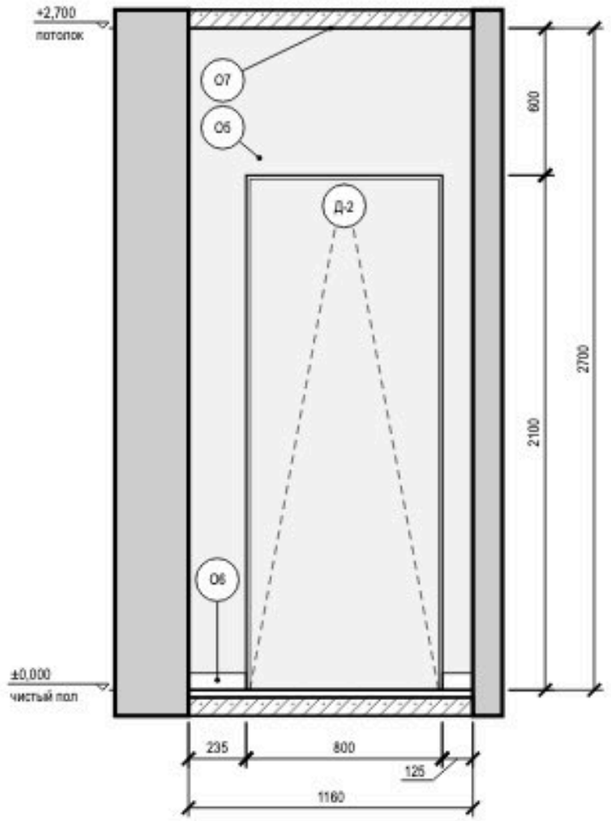


Схема развёрток (М 1:100)



Условные обозначения

- розетка с заземляющим контактом; у знака — марка, ×N постов в рамке, гр. — группа щита, H — высота оси, мм
- выключатель одноклавишный
- выключатель с проходной или перекрёстной клавишей (обратный флажок); тип клавиши — в подписи
- привязки точек и выводов от угла и от пола, мм
- мебель и приборы — фасад по расстановке (условно)
- дверь скрытого монтажа: полотно в плоскости стены (узел — на листе узлов)
- дверной проём; марка двери — в кружке
- стены и перекрытия в сечении
- О1 — марка отделки по реестру отделки альбома
- А — марка развёртки: буква стены, стрелка — взгляд

Ведомость отделки (на листе)

Марка	Поверхность	Материал, изделие	Цвет, код	Кол.
О5	стены	окраска, Tikkurila, шелковисто-матовая, подготовка Q3	NCS S 1502-Y50R	11,4 м²
О6	плинтус	плинтус МДФ, Orac Decor Contour (Luxxus), h 69 мм, SX165, шелковисто-матовая	NCS S 0300-N	3,8 м
О7	потолок	окраска, Tikkurila, глубокоматовая	NCS S 0300-N	5,5 м²

Допущения и предложения на листе

Основа листа: размеры сняты с растрового плана заказчика без размеров; масштаб восстановлен по площадям помещений (≈ 11,8 мм на пиксель), контрольный обмер не выполнен (К-1); высота потолка 2700 мм принята: на плане заказчика её нет (К-2); толщины стен 300 / 120 мм приняты по плану заказчика, не замерены (К-1); разрешённая мощность 15 кВт принята по типовым ТУ для квартиры, ТУ заказчиком не переданы (К-4). См. лист открытых вопросов (лист 5, записи К-1, К-2, К-4).

Примечания

1. Развёртки — вид на стену изнутри помещения, по часовой стрелке; расположение — на схеме листа и на листе 54; размеры — в мм по чистовым поверхностям; отметки — в м от ±0,000; высоты H — от чистого пола помещения до оси изделия, у декора — до центра.
2. Красные цепочки — привязки электроточек и выводов: по горизонтали от угла чистовых стен, по вертикали от чистого пола, до оси изделия; звенья короче 3 мм на листе вынесены во второй ярус (ближние к стене цепочка).
3. У знака электроточки: марка (Р — розетка, S — выключатель, Св — светильник, ЭВ — вывод кабеля), ×N — число постов в рамке, гр. — группа щита, H — высота оси от чистого пола, мм; группы по клавишам выключателя — на листе выключателей.
4. Схема мебели, приборов и декора не является технической документацией для производства мебели; габариты — по паспортам изделий.
5. Двери скрытого монтажа — полотно в плоскости стены, отделка стены по полотну, плинтус прерывается у короба (узел — на листе узлов).

1000 мм · печать 1:1

Изм.	Кол.уч	Лист	№ док.	Подп.	Дата
Разраб.		Кырпан А.С.			09.10.26
Пров.					
ГИП					
Н. контр.					
Утв.					

ГД-2026-007-АИ

Квартира 65 м²

Общая площадь 65,24* м² · * размеры со скана, не замерены (реестр — п. 5, К-1)

Дизайн-проект интерьера

Стадия	Лист	Листов
РП	63	79

Развёртки стен А, Б. Коридор (пом. 5)

М 1:25

Кырпан Александр Сергеевич


выпуск 09.10.2026 № 147dabfd23 · стр. 74 из 110

Развёртки стен В, Г. Коридор (пом. 5)

Коридор (пом. 5) · вид изнутри помещения · размеры в мм, отметки в м

ПРЕДВАРИТЕЛЬНО · не для производства работ · открыто пунктов: 4 (реестр — л. 5)

Развёртка стены В

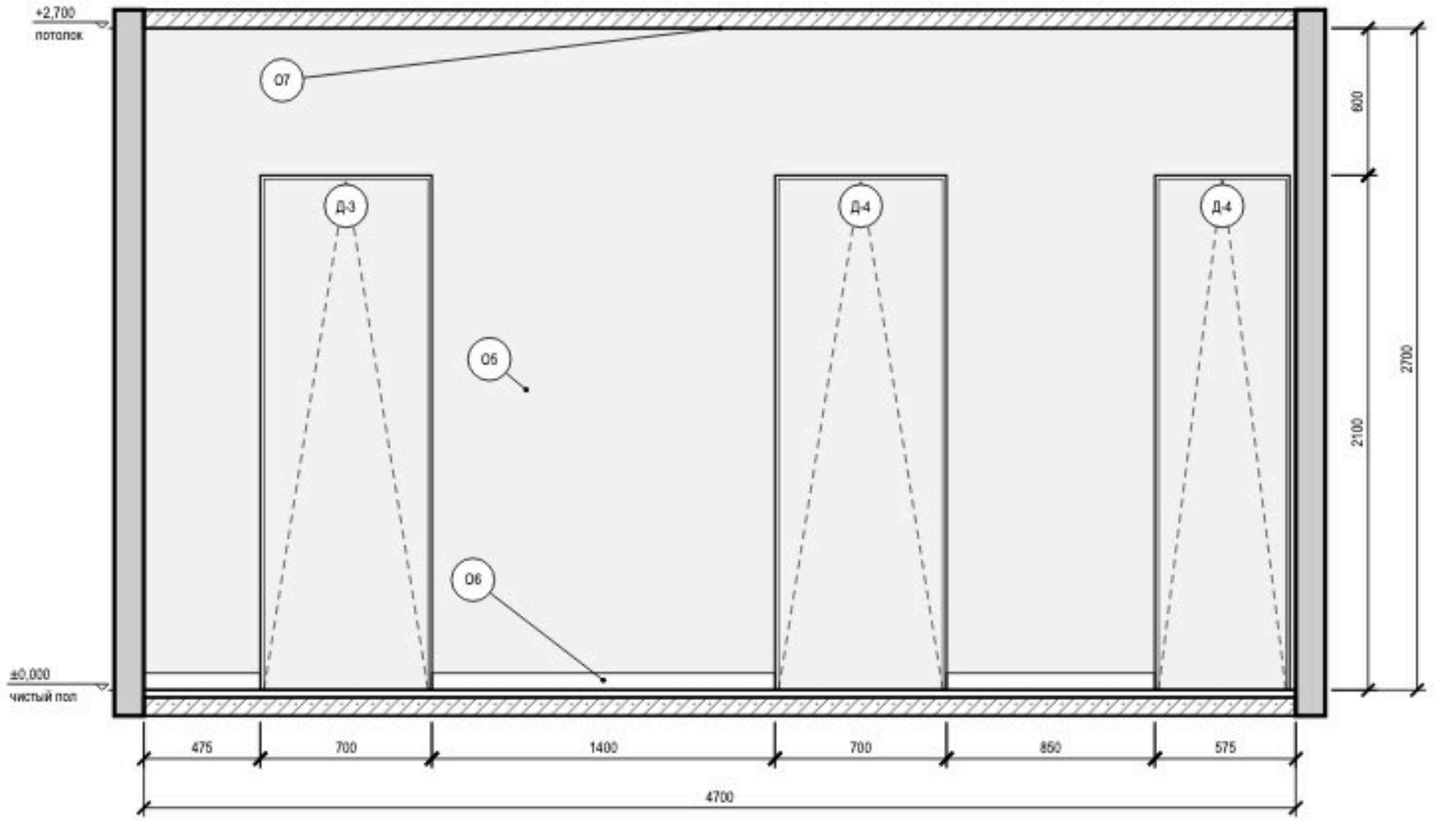

Развёртка стены Г

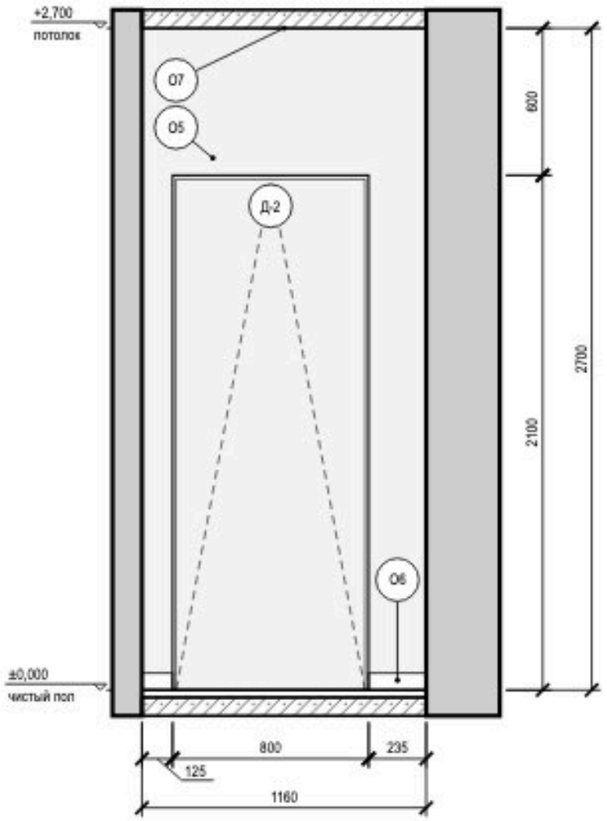


Схема развёрток (М 1:100)



Условные обозначения

- привязки точек и выводов от угла и от пола, мм
- мебель и приборы — фасад по расстановке (условно)
- дверь скрытого монтажа: полотно в плоскости стены (узел — на листе узлов)
- стены и перекрытия в сечении
- О1 — марка отделки по реестру отделки альбома
- А — марка развёртки: буква стены, стрелка — взгляд

Ведомость отделки (на листе)

Марка	Поверхность	Материал, изделие	Цвет, код	Кол.
О5	стены	окраска, Tikkurila, шелковисто-матовая, подготовка Q3	NCS S 1502-Y50R	10 м²
О6	плинтус	плинтус МДФ, Orac Decor Contour (Luxxus), h 69 мм, SX165, шелковисто-матовая	NCS S 0300-N	3,1 м
О7	потолок	окраска, Tikkurila, глубокоматовая	NCS S 0300-N	5,5 м²

Допущения и предложения на листе

Основа листа: размеры сняты с растрового плана заказчика без размеров: масштаб восстановлен по площадям помещений (≈ 11,8 мм на пиксель), контрольный обмер не выполнен (К-1); высота потолка 2700 мм принята: на плане заказчика её нет (К-2); толщины стен 300 / 120 мм приняты по плану заказчика, не замерены (К-1); разрешённая мощность 15 кВт принята по типовым ТУ для квартиры, ТУ заказчиком не переданы (К-4).
См. лист открытых вопросов (лист 5, записи К-1, К-2, К-4).

Примечания

1. Развёртки — вид на стену изнутри помещения, по часовой стрелке; расположение — на схеме листа и на листе 54; размеры — в мм по чистовым поверхностям; отметки — в м от ±0,000; высоты Н — от чистого пола помещения до оси изделия, у декора — до центра.
2. Красные цепочки — привязки электроточек и выводов: по горизонтали от угла чистовых стен, по вертикали от чистого пола, до оси изделия; звенья короче 3 мм на листе вынесены во второй ярус (ближняя к стене цепочка).
3. У знака электроточки: марка (Р — розетка, S — выключатель, Св — светильник, ЭВ — вывод кабеля), ×N — число постов в рамке, гр. — группа щита, Н — высота оси от чистого пола, мм; группы по клавишам выключателя — на листе выключателей.
4. Схема мебели, приборов и декора не является технической документацией для производства мебели; габариты — по паспортам изделий.
5. Двери скрытого монтажа — полотно в плоскости стены, отделка стены по полотну, плинтус прерывается у короба (узел — на листе узлов).

1000 мм · печать 1:1

Изм.	Кол.уч	Лист	№ док.	Подп.	Дата
Разраб.		Кырпан А.С.			09.10.26
Пров.					
ГИП					
Н. контр.					
Утв.					

ГД-2026-007-АИ

Квартира 65 м²

Общая площадь 65,24* м² · * размеры со скана, не замерены (реестр — п. 5, К-1)

Дизайн-проект интерьера

Стадия	Лист	Листов
РП	64	79

Развёртки стен В, Г. Коридор (пом. 5)

М 1:25

Кырпан Александр Сергеевич


выпуск 09.10.2026 № 147dabfd23 · стр. 75 из 110

Развёртки стен А, Б. Санузел (пом. 6)

Санузел (пом. 6) · вид изнутри помещения · размеры в мм, отметки в м

ПРЕДВАРИТЕЛЬНО · не для производства работ · открыто пунктов: 4 (реестр — л. 5)

Развёртка стены А

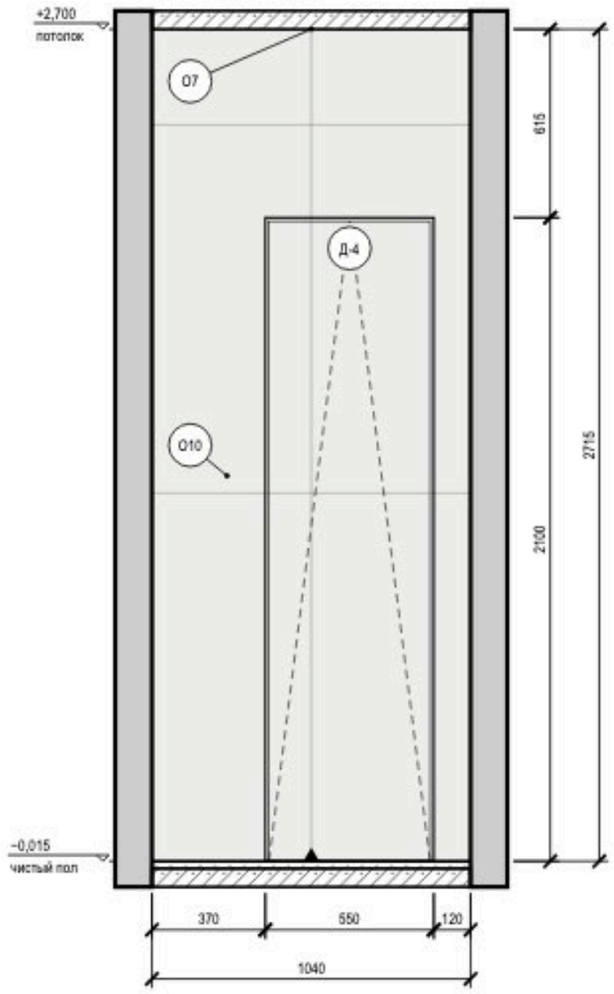

Развёртка стены Б

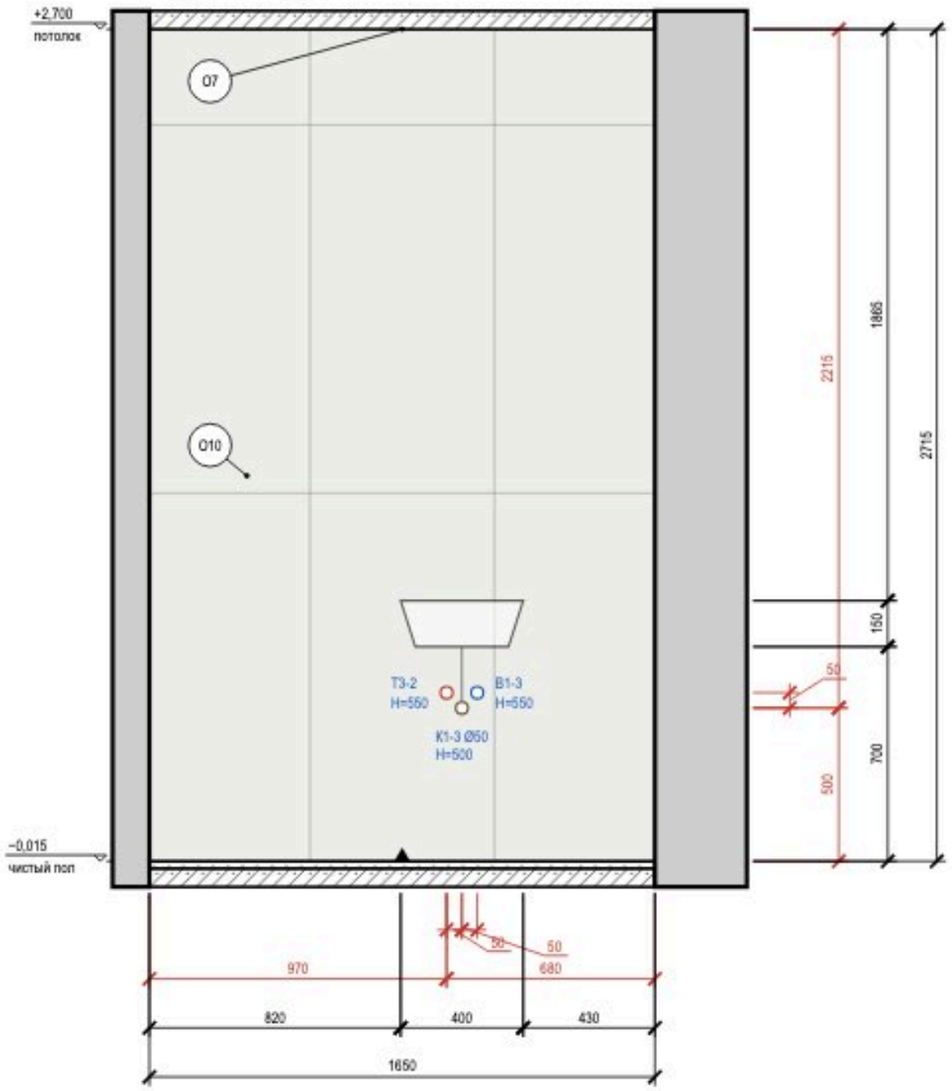


Схема развёрток (М 1:100)



Условные обозначения

- вывод В1 (код — в ведомости привязок)
- вывод Т3 (код — в ведомости привязок)
- вывод К1 (код — в ведомости привязок)
- привязки точек и выводов от угла и от пола, мм
- мебель и приборы — фасад по расстановке (условно)
- дверь скрытого монтажа: полотно в плоскости стены (узел — на листе узлов)
- стены и перекрытия в сечении
- плитка: сетка швов по формату, ▲ — ось старта
- О1 — марка отделки по реестру отделки альбома
- А — марка развёртки: буква стены, стрелка — взгляд

Ведомость отделки (на листе)

Марка	Поверхность	Материал, изделие	Цвет, код	Кол.
О7	потолок	окраска, Tikkurila, глубокоматовая	NCS S 0300-N	1,8 м²
О10	стены	облицовка плиткой, Italon Charme Extra, 600×1200 мм, 610010001196	Italon 610010001195 «Charme Extra»	6,1 м²

Допущения и предложения на листе

Основа листа: размеры сняты с растрового плана заказчика без размеров: масштаб восстановлен по площадям помещений (≈ 11,8 мм на гиксель), контрольный обмер не выполнен (К-1); высота потолка 2700 мм принята: на плане заказчика её нет (К-2); толщины стен 300 / 120 мм приняты по плану заказчика, не замерены (К-1); разрешённая мощность 15 кВт принята по типовым ТУ для квартиры, ТУ заказчиком не переданы (К-4).

См. лист открытых вопросов (лист 5, записи К-1, К-2, К-4).

Примечания

1. Развёртки — вид на стену изнутри помещения, по часовой стрелке; расположение — на схеме листа и на листе 54; размеры — в мм по чистовым поверхностям; отметки — в м от ±0,000; высоты Н — от чистого пола помещения до оси изделия, у декора — до центра.
2. Красные цепочки — привязки электроточек и выводов: по горизонтали от угла чистовых стен, по вертикали от чистого пола, до оси изделия; звенья короче 3 мм на листе вынесены во второй ярус (ближняя к стене цепочка).
3. У знака электроточки: марка (Р — розетка, S — выключатель, Св — светильник, ЭВ — вывод кабеля), ×N — число постов в рамке, гр. — группа щита, Н — высота оси от чистого пола, мм; группы по клавишам выключателя — на листе выключателей.
4. Схема мебели, приборов и декора не является технической документацией для производства мебели; габариты — по паспортам изделий.
5. Облицовка — по сетке швов, раскладка от оси стены (треугольник у пола); подрезки — по листу раскладки плитки.
6. Гидроизоляция в 2 слоя, заход на стены 200 мм — до облицовки, с актом скрытых работ и тестом проливом (узел — на листе узлов).
7. Двери скрытого монтажа — полотно в плоскости стены, отделка стены по полотну, плинтус прерывается у короба (узел — на листе узлов).

1000 мм · печать 1:1

Изм.	Кол.уч	Лист	№ док.	Подп.	Дата
Разраб.		Кырпан А.С.			09.10.26
Пров.					
ГИП					
Н. контр.					
Утв.					

ГД-2026-007-АИ

Квартира 65 м²

Общая площадь 65,24* м² · * размеры со скана, не замерены (реестр — п. 5, К-1)

Дизайн-проект интерьера	Стадия	Лист	Листов
	РП	65	79

Развёртки стен А, Б. Санузел (пом. 6)

М 1:20

Кырпан Александр Сергеевич


выпуск 09.10.2026 № 147dabfd23 · стр. 76 из 110

Развёртки стен В, Г. Санузел (пом. 6)

Санузел (пом. 6) · вид изнутри помещения · размеры в мм, отметки в м

ПРЕДВАРИТЕЛЬНО · не для производства работ · открыто пунктов: 4 (реестр — л. 5)

Развёртка стены В

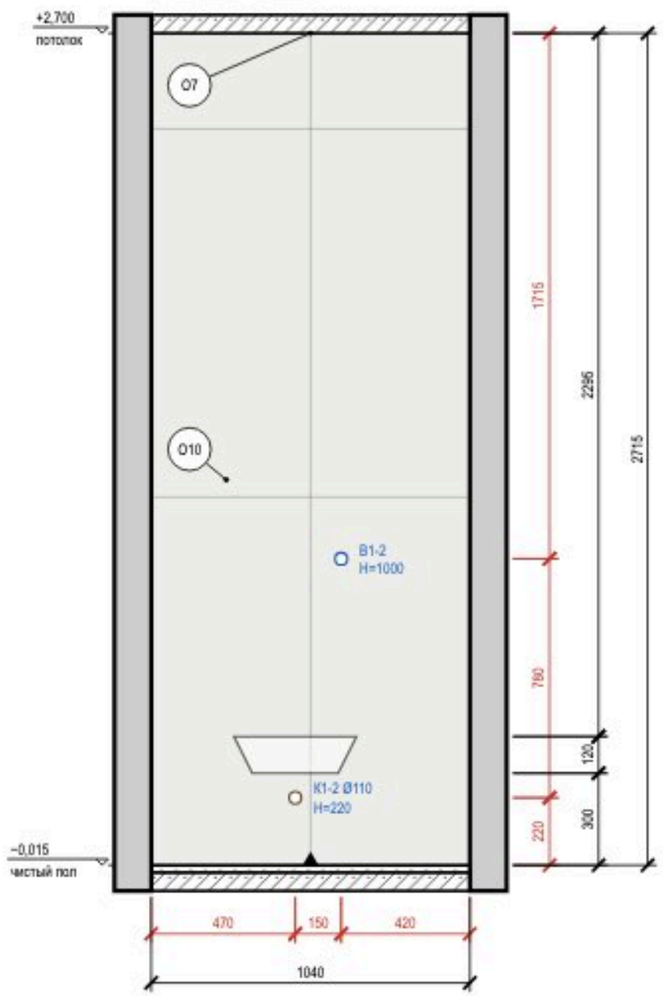

Развёртка стены Г


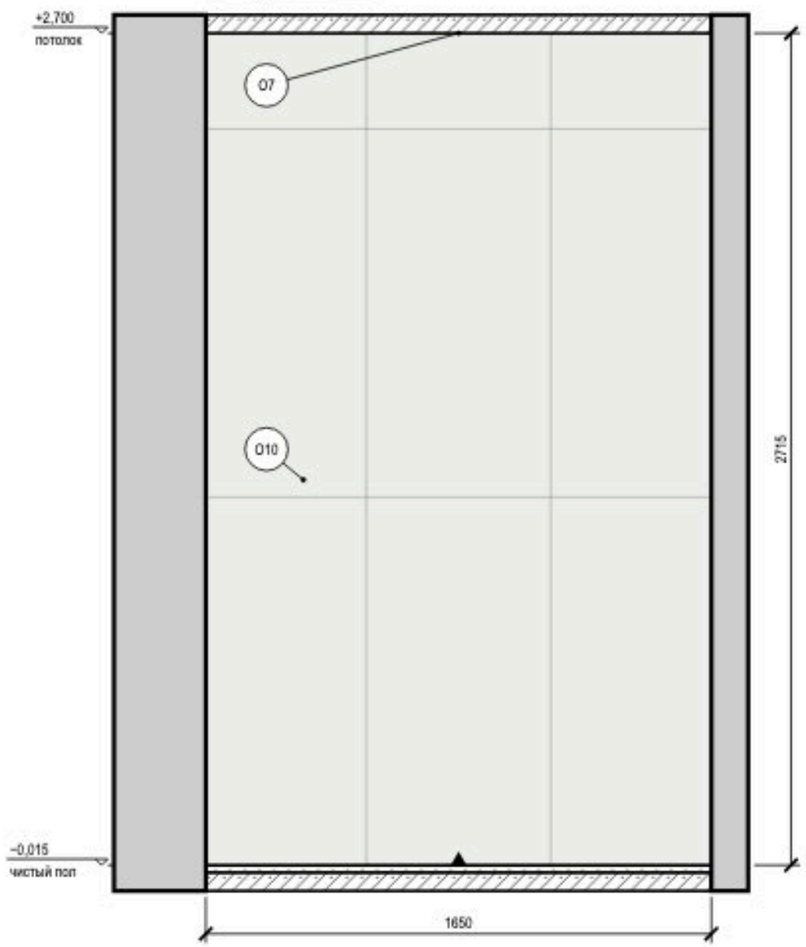


Схема развёрток (М 1:100)

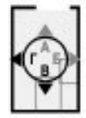

Условные обозначения

- вывод В1 (код — в ведомости привязок)
- вывод К1 (код — в ведомости привязок)
- привязки точек и выводов от угла и от пола, мм
- мебель и приборы — фасад по расстановке (условно)
- стены и перекрытия в сечении
- плитка: сетка швов по формату, ▲ — ось старта
- О1 — марка отделки по реестру отделки альбома
- А — марка развёртки: буква стены, стрелка — взгляд

Ведомость отделки (на листе)

Марка	Поверхность	Материал, изделие	Цвет, код	Кол.
О7	потолок	окраска, Tikkurila, глубокоматовая	NCS S 0300-N	1,8 м²
О10	стены	облицовка плиткой, Italon Charme Extra, 600×1200 мм, 610010001195	Italon 610010001195 «Charme Extra»	7,3 м²

Допущения и предложения на листе

Основа листа: размеры сняты с растрового плана заказчика без размеров: масштаб восстановлен по площадям помещений (≈ 11,8 мм на пиксель), контрольный обмер не выполнен (К-1); высота потолка 2700 мм принята: на плане заказчика её нет (К-2); толщины стен 300 / 120 мм приняты по плану заказчика, не замерены (К-1); разрешённая мощность 15 кВт принята по типовым ТУ для квартиры, ТУ заказчиком не переданы (К-4).

См. лист открытых вопросов (лист 5, записи К-1, К-2, К-4).

Примечания

1. Развёртки — вид на стену изнутри помещения, по часовой стрелке; расположение — на схеме листа и на листе 54; размеры — в мм по чистовым поверхностям; отметки — в м от ±0,000; высоты Н — от чистого пола помещения до оси изделия, у декора — до центра.
2. Красные цепочки — привязки электроточек и выводов: по горизонтали от угла чистовых стен, по вертикали от чистого пола, до оси изделия; звенья короче 3 мм на листе вынесены во второй ярус (ближняя к стене цепочка).
3. У знака электроточки: марка (Р — розетка, S — выключатель, Св — светильник, ЭВ — вывод кабеля), ×N — число постов в рамке, гр. — группа щита, Н — высота оси от чистого пола, мм; группы по клавишам выключателя — на листе выключателей.
4. Схема мебели, приборов и декора не является технической документацией для производства мебели; габариты — по паспортам изделий (* — высота не задана в проекте, показана по типовому изделию).
5. Облицовка — по сетке швов, раскладка от оси стены (треугольник у пола); подрезки — по листу раскладки плитки.
6. Гидроизоляция в 2 слоя, заход на стены 200 мм — до облицовки, с актом скрытых работ и тестом проливом (узел — на листе узлов).

1000 мм · печать 1:1

Изм.	Кол.уч	Лист	№ док.	Подп.	Дата
Разраб.		Кырпан А.С.			09.10.26
Пров.					
ГИП					
Н. контр.					
Утв.					

ГД-2026-007-АИ

Квартира 65 м²

Общая площадь 65,24* м² · * размеры со скана, не замерены (реестр — л. 5, К-1)

Дизайн-проект интерьера

Стадия	Лист	Листов
РП	66	79

Развёртки стен В, Г. Санузел (пом. 6)

М 1:20

Кырпан Александр Сергеевич


выпуск 09.10.2026 · 147dabfd23 · стр. 77 из 110

Развёртки стен А, Б. Ванная (пом. 7)


Ванная (пом. 7) · вид изнутри помещения · размеры в мм, отметки в м

ПРЕДВАРИТЕЛЬНО · не для производства работ · открыто пунктов: 4 (реестр — л. 5)

Развёртка стены А

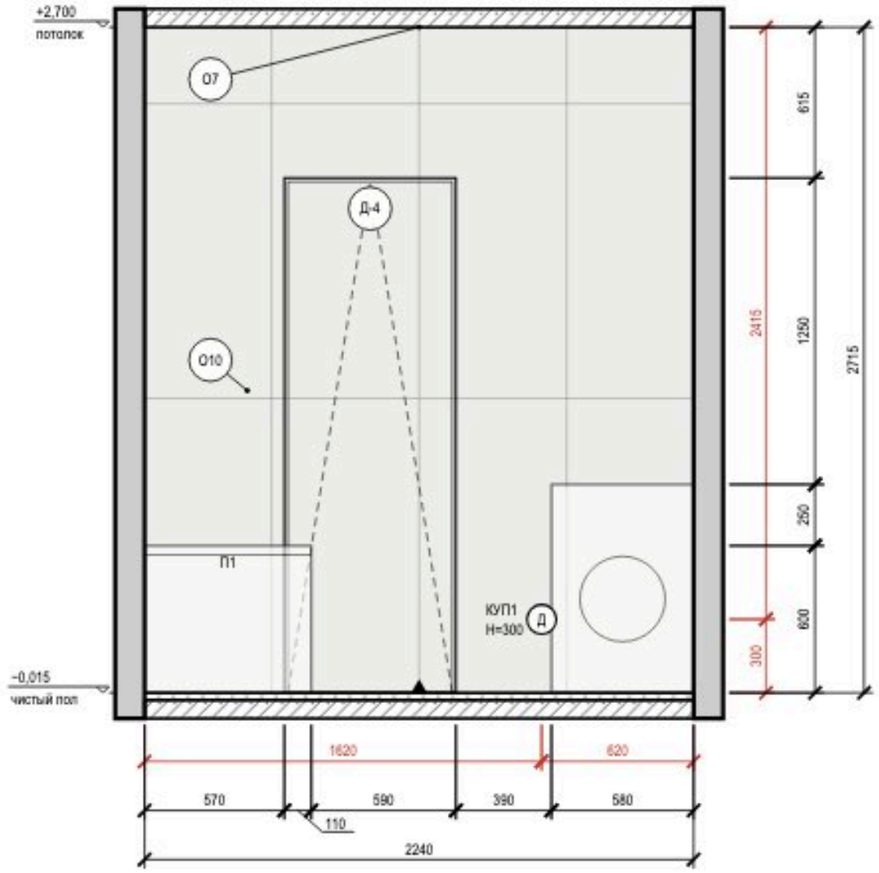


Развёртка стены Б

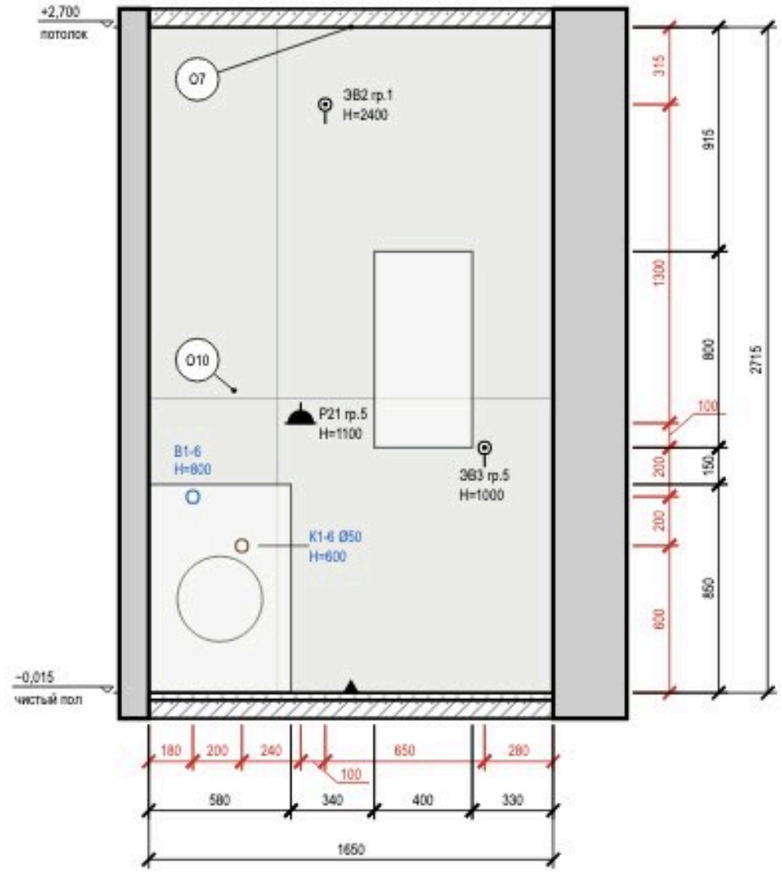

Условные обозначения

- розетка влагозащищённая IP44
- вывод кабеля для подключения прибора (без розетки), марка ЭВ
- вывод В1 (код — в ведомости привязок)
- вывод К1 (код — в ведомости привязок)
- привязки точек и выводов от угла и от пола, мм
- мебель и приборы — фасад по расстановке (условно)
- дверь скрытого монтажа: полотно в плоскости стены (узел — на листе узлов)
- стены и перекрытия в сечении
- плитка: сетка швов по формату, ▲ — ось старта
- О1 — марка отделки по реестру отделки альбома
- А — марка развёртки: буква стены, стрелка — взгляд

Схема развёрток (М 1:100)

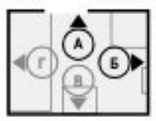

Ведомость отделки (на листе)

Марка	Поверхность	Материал, изделие	Цвет, код	Кол.
О7	потолок	окраска, Tikkurila, глубокоматовая	NCS S 0300-N	3,9 м²
О10	стены	облицовка плиткой, Italon Charme Extra, 600×1200 мм, 610010001195	Italon 610010001195 «Charme Extra»	9,1 м²

Допущения и предложения на листе

Основа листа: размеры сняты с растрового плана заказчика без размеров: масштаб восстановлен по площадям помещений (≈ 11,8 мм на пиксель), контрольный обмер не выполнен (К-1); высота потолка 2700 мм принята: на плане заказчика её нет (К-2); толщины стен 300 / 120 мм приняты по плану заказчика, не замерены (К-1); разрешённая мощность 15 кВт принята по типовым ТУ для квартиры, ТУ заказчиком не переданы (К-4).

См. лист открытых вопросов (лист 5, записи К-1, К-2, К-4).

Примечания

1. Развёртки — вид на стену изнутри помещения, по часовой стрелке; расположение — на схеме листа и на листе 54; размеры — в мм по чистовым поверхностям; отметки — в м от ±0,000; высоты Н — от чистого пола помещения до оси изделия, у декора — до центра.
2. Красные цепочки — привязки электроточек и выводов: по горизонтали от угла чистовых стен, по вертикали от чистого пола, до оси изделия; звенья короче 3 мм на листе вынесены во второй ярус (ближняя к стене цепочка).
3. У знака электроточки: марка (Р — розетка, S — выключатель, Св — светильник, ЭВ — вывод кабеля), ×N — число постов в рамке, гр. — группа щита, Н — высота оси от чистого пола, мм; группы по клавишам выключателя — на листе выключателей.
4. Схема мебели, приборов и декора не является технической документацией для производства мебели; габариты — по паспортам изделий (* — высота не задана в проекте, показана по типовому изделию).
5. Облицовка — по сетке швов, раскладка от оси стены (треугольник у пола); подрезки — по листу раскладки плитки.
6. Гидроизоляция в 2 слоя, заход на стены 200 мм — до облицовки, с актом скрытых работ и тестом проливом (узел — на листе узлов).
7. Двери скрытого монтажа — полотно в плоскости стены, отделка стены по полотну, плинтус прерывается у короба (узел — на листе узлов).

1000 мм · печать 1:1

Изм.	Кол.уч	Лист	№ док.	Подп.	Дата
Разраб.		Кырпан А.С.			09.10.26
Пров.					
ГИП					
Н. контр.					
Утв.					

ГД-2026-007-АИ

Квартира 65 м²

Общая площадь 65,24* м² · * размеры со скана, не замерены (реестр — п. 5, К-1)

Дизайн-проект интерьера

Стадия	Лист	Листов
РП	67	79

Развёртки стен А, Б. Ванная (пом. 7)

М 1:25

Кырпан Александр Сергеевич


выпуск 09.10.2026 · 147dabfd23 · стр. 78 из 110

Развёртки стен В, Г. Ванная (пом. 7)


Ванная (пом. 7) · вид изнутри помещения · размеры в мм, отметки в м

ПРЕДВАРИТЕЛЬНО · не для производства работ · открыто пунктов: 4 (реестр — л. 5)

Развёртка стены В

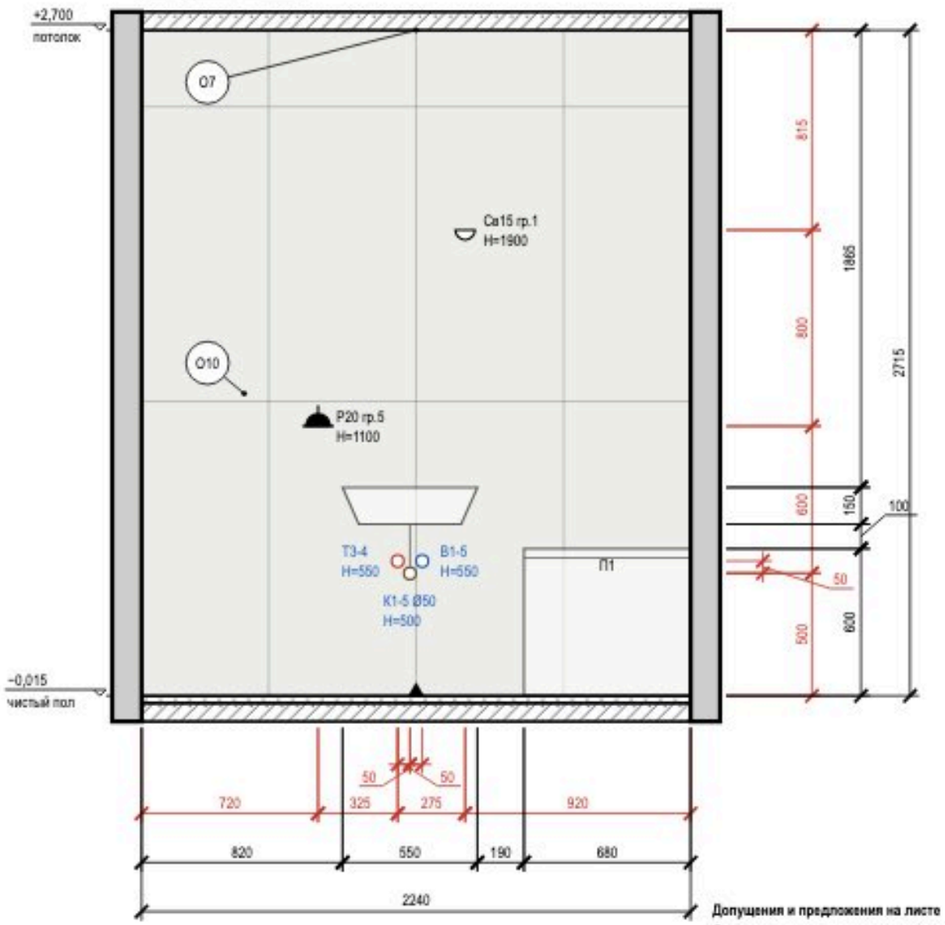


Развёртка стены Г

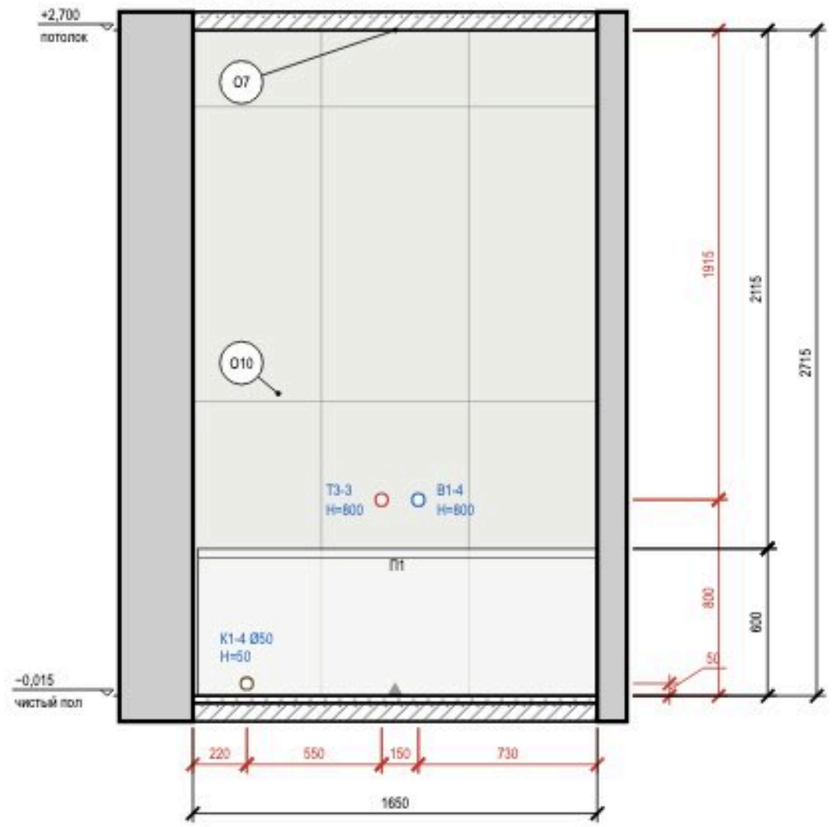

Условные обозначения

- розетка влагозащищённая IP44
- светильник настенный (бра), H — высота оси
- вывод В1 (код — в ведомости привязок)
- вывод Т3 (код — в ведомости привязок)
- вывод К1 (код — в ведомости привязок)
- привязки точек и выводов от угла и от пола, мм
- мебель и приборы — фасад по расстановке (условно)
- стены и перекрытия в сечении
- плитка: сетка швов по формату, ▲ — ось старта
- О1 — марка отделки по реестру отделки альбома
- А — марка развёртки: буква стены, стрелка — взгляд

Схема развёрток (М 1:100)

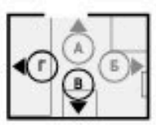

Ведомость отделки (на листе)

Марка	Поверхность	Материал, изделие	Цвет, код	Кол.
О7	потолок	окраска, Tikkurila, глубокоматовая	NCS S 0300-N	3,9 м²
О10	стены	облицовка плиткой, Italon Charme Extra, 600×1200 мм, 610010001196	Italon 610010001195 «Charme Extra»	10,6 м²

Допущения и предложения на листе

Основа листа: размеры сняты с растрового плана заказчика без размеров; масштаб восстановлен по площадям помещений (≈ 11,8 мм на пиксель), контрольный обмер не выполнен (К-1); высота потолка 2700 мм принята: на плане заказчика её нет (К-2); толщины стен 300 / 120 мм приняты по плану заказчика, не замерены (К-1); разрешённая мощность 15 кВт принята по типовым ТУ для квартиры, ТУ заказчиком не переданы (К-4).

См. лист открытых вопросов (лист 5, записи К-1, К-2, К-4).

Примечания

1. Развёртки — вид на стену изнутри помещения, по часовой стрелке; расположение — на схеме листа и на листе 54; размеры — в мм по чистовым поверхностям; отметки — в м от ±0,000; высоты H — от чистого пола помещения до оси изделия, у декора — до центра.
2. Красные цепочки — привязки электроточек и выводов: по горизонтали от угла чистовых стен, по вертикали от чистого пола, до оси изделия; звенья короче 3 мм на листе вынесены во второй ярус (ближняя к стене цепочка).
3. У знака электроточки: марка (Р — розетка, S — выключатель, Св — светильник, ЭВ — вывод кабеля), ×N — число постов в рамке, гр. — группа щита, H — высота оси от чистого пола, мм; группы по клавишам выключателя — на листе выключателей.
4. Схема мебели, приборов и декора не является технической документацией для производства мебели; габариты — по паспортам изделий.
5. Облицовка — по сетке швов, раскладка от оси стены (треугольник у пола); подрезки — по листу раскладки плитки.
6. Гидроизоляция в 2 слоя, заход на стены 200 мм — до облицовки, с актом скрытых работ и тестом проливом (узел — на листе узлов).

1000 мм · печать 1:1

Изм.	Кол.уч	Лист	№ док.	Подп.	Дата
Разраб.		Кырпан А.С.			09.10.26
Пров.					
ГИП					
Н. контр.					
Утв.					

ГД-2026-007-АИ

Квартира 65 м²

Общая площадь 65,24* м² · * размеры со скана, не замерены (реестр — п. 5, К-1)

Дизайн-проект интерьера

Стадия	Лист	Листов
РП	68	79

Развёртки стен В, Г. Ванная (пом. 7)

М 1:25

Кырпан Александр Сергеевич


выпуск 09.10.2026 · 147dabfd23 · стр. 79 из 110

Развёртки стен. Кладовая (пом. 8)


Кладовая (пом. 8) · вид изнутри помещения · размеры в мм, отметки в м

ПРЕДВАРИТЕЛЬНО · не для производства работ · открыто пунктов: 4 (реестр — л. 5)

Развёртка стены А

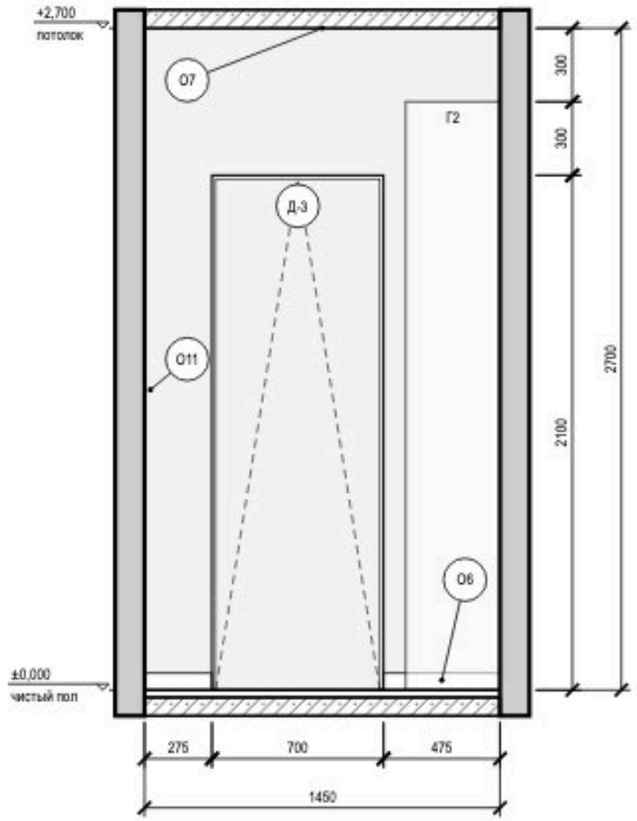

Развёртка стены Б

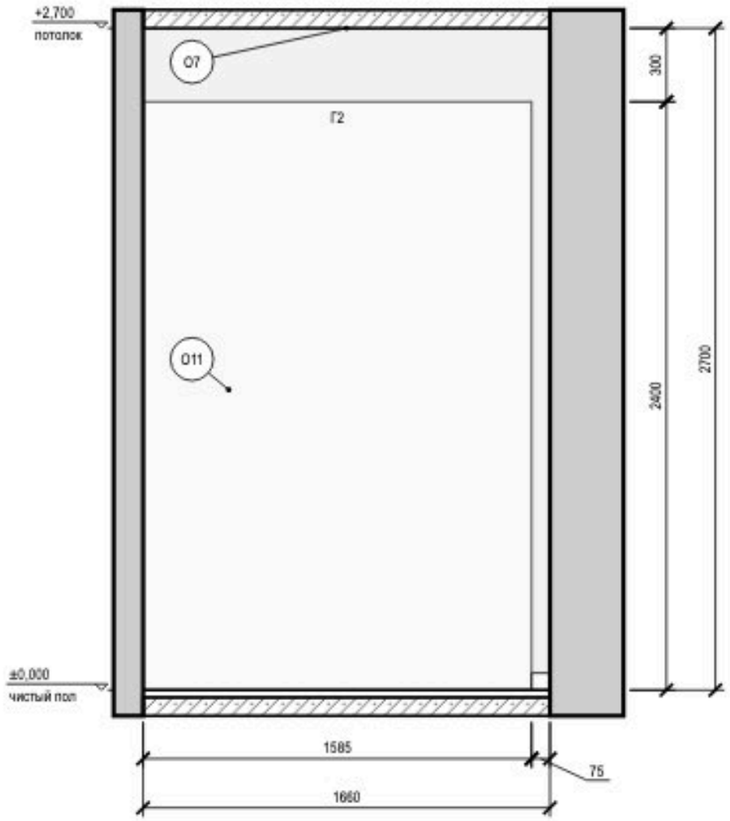

Развёртка стены В


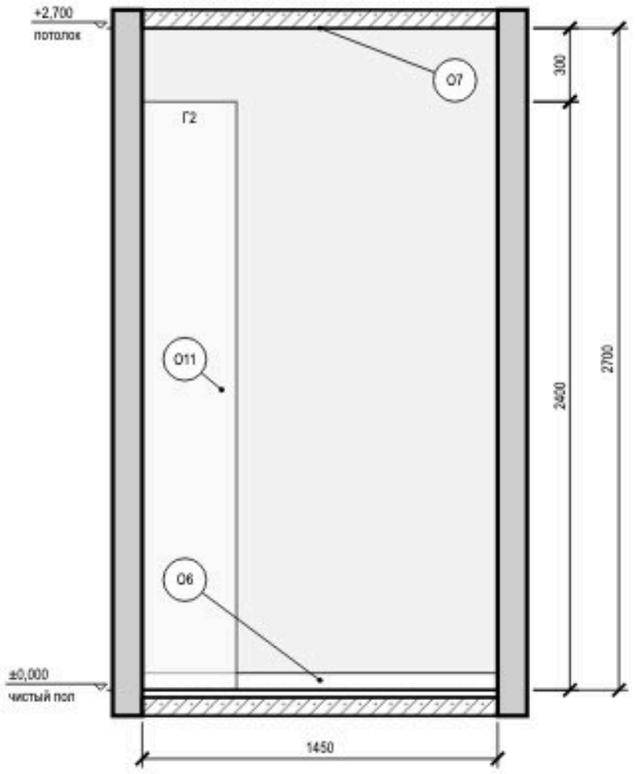


Схема развёрток (М 1:100)

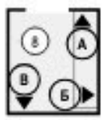

Условные обозначения

привязки точек и выводов от угла и от пола, мм

мебель и приборы — фасад по расстановке (условно)

дверь скрытого монтажа: полотно в плоскости стены (узел — на листе узлов)

стены и перекрытия в сечении

О1 — марка отделки по реестру отделки альбома

А — марка развёртки: буква стены, стрелка — взгляд

Ведомость отделки (на листе)

Марка	Поверхность	Материал, изделие	Цвет, код	Кол.
О6	плинтус	плинтус МДФ, Orac Decor Contour (Luxxus), h 69 мм, SX165, шелковисто-матовая	NCS S 0300-N	2,3 м
О7	потолок	окраска, Tikkurila, глубокоматовая	NCS S 0300-N	2,6 м²
О11	стены	окраска, Tikkurila, матовая, подготовка Q3	NCS S 0502-Y	10,8 м²

Допущения и предложения на листе

Основа листа: размеры сняты с растрового плана заказчика без размеров: масштаб восстановлен по площадям помещений (≈ 11,8 мм на пиксель), контрольный обмер не выполнен (К-1); высота потолка 2700 мм принята: на плане заказчика её нет (К-2); толщины стен 300 / 120 мм приняты по плану заказчика, не замерены (К-1); разрешённая мощность 15 кВт принята по типовым ТУ для квартиры, ТУ заказчиком не переданы (К-4).

См. лист открытых вопросов (лист 5, записи К-1, К-2, К-4).

Примечания

1. Развёртки — вид на стену изнутри помещения, по часовой стрелке; расположение — на схеме листа и на листе 54; размеры — в мм по чистовым поверхностям; отметки — в м от ±0,000; высоты Н — от чистого пола помещения до оси изделия, у декора — до центра.
2. Красные цепочки — привязки электроточек и выводов: по горизонтали от угла чистовых стен, по вертикали от чистого пола, до оси изделия; звенья короче 3 мм на листе вынесены во второй ярус (ближняя к стене цепочка).
3. У знака электроточки: марка (Р — розетка, S — выключатель, Св — светильник, ЭВ — вывод кабеля), ×N — число постов в рамке, гр. — группа щита, Н — высота оси от чистого пола, мм; группы по клавишам выключателя — на листе выключателей.
4. Схема мебели, приборов и декора не является технической документацией для производства мебели; габариты — по паспортам изделий.
5. Двери скрытого монтажа — полотно в плоскости стены, отделка стены по полотну, плинтус прерывается у короба (узел — на листе узлов).

1000 мм · печать 1:1

Изм.	Кол.уч	Лист	№ док.	Подп.	Дата
Разраб.		Кырлан А.С.			09.10.26
Пров.					
ГИП					
Н. контр.					
Утв.					

ГД-2026-007-АИ

Квартира 65 м²

Общая площадь 65,24* м² · * размеры со скана, не замерены (реестр — п. 5, К-1)

Дизайн-проект интерьера

Стадия	Лист	Листов
РП	69	79

Развёртки стен. Кладовая (пом. 8)

М 1:25


Кырлан Александр Сергеевич

выпуск 09.10.2026 № 147dabfd23 · стр. 80 из 110

Развёртки стен А, Б. Детская (пом. 9)

Детская (пом. 9) · вид изнутри помещения · размеры в мм, отметки в м

Развёртка стены А

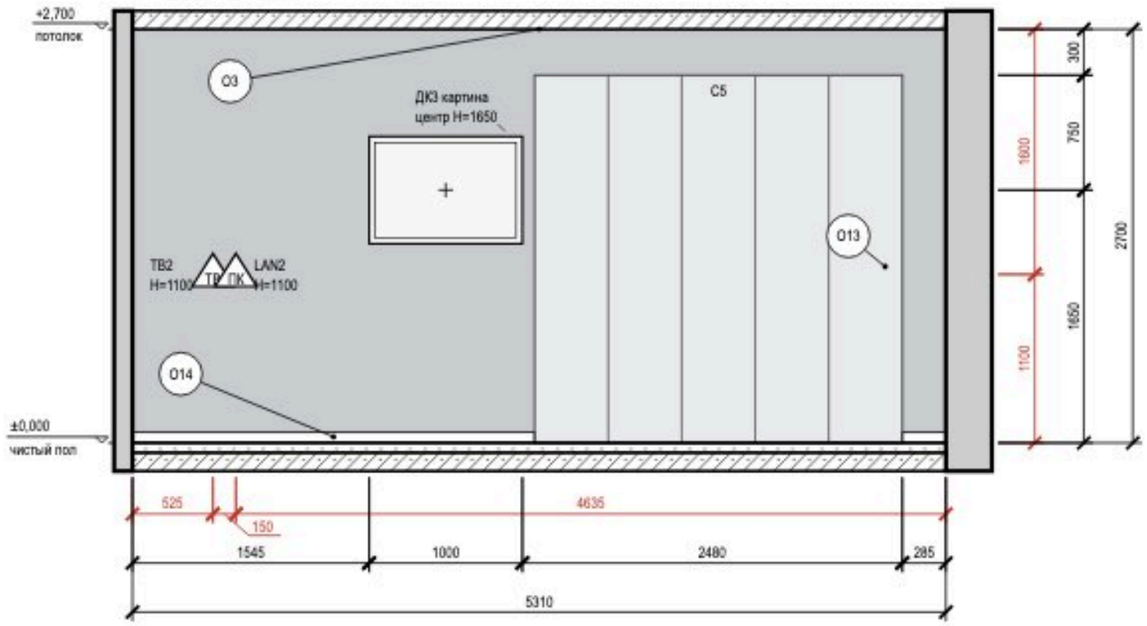

Развёртка стены Б


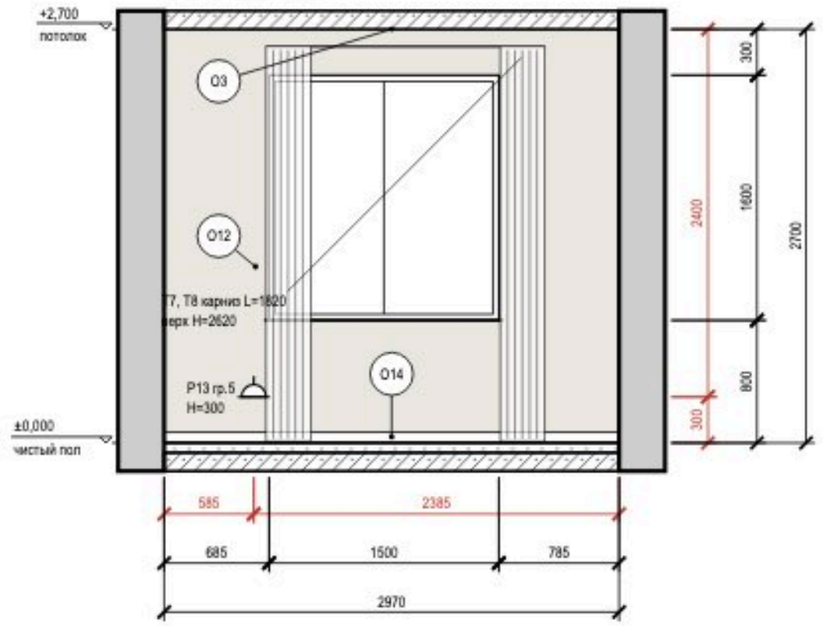


Схема развёрток (М 1:100)

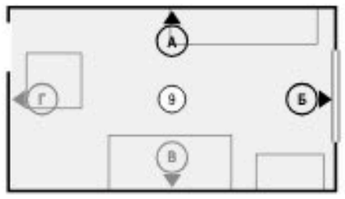

Условные обозначения

- розетка с заземляющим контактом; у знака — марка, ×N постов в рамке, гр. — группа щита, Н — высота оси, мм
- розетка компьютерная RJ45
- розетка телевизионная
- привязки точек и выводов от угла и от пола, мм
- мебель и приборы — фасад по расстановке (условно)
- картина (декор): марка Д, крест — центр, Н — высота центра, мм
- карниз (шина) и шторы в собранном виде: марка Т, длина L, верх Н
- окно: проём, рама, подоконник
- стены и перекрытия в сечении
- окраска: тон — цвет по коду производителя (условно)
- О1 — марка отделки по реестру отделки альбома
- А — марка развёртки: буква стены, стрелка — взгляд

Ведомость отделки (на листе)

Марка	Поверхность	Материал, изделие	Цвет, код	Кол.
О3	потолок	окраска, Tikkurila Anti-Reflex 2, глубокоматовая, подготовка Q3	Tikkurila V503 «Winter»	16 м²
О12	стены	окраска, Farrow & Ball Modern Emulsion, матовая, подготовка Q3	Farrow & Ball No. 241 «Skimming Stone»	5,6 м²
О13	акцентная стена	окраска, Farrow & Ball Modern Emulsion, матовая, подготовка Q3	Farrow & Ball No. 30 «Hague Blue»	14,3 м²
О14	плинтус	плинтус МДФ, Orac Decor Contour (Luxxus), h 69 мм, SX165	Farrow & Ball No. 241 «Skimming Stone»	5,9 м

Допущения и предложения на листе

Основа листа: размеры сняты с растрового плана заказчика без размеров: масштаб восстановлен по площадям помещений (≈ 11,8 мм на пиксель), контрольный обмер не выполнен (К-1); высота потолка 2700 мм принята: на плане заказчика её нет (К-2); толщины стен 300 / 120 мм приняты по плану заказчика, не замерены (К-1); разрешённая мощность 15 кВт принята по типовым ТУ для квартиры, ТУ заказчиком не переданы (К-4).
См. лист открытых вопросов (лист 5, записи К-1, К-2, К-4).

Примечания

1. Развёртки — вид на стену изнутри помещения, по часовой стрелке; расположение — на схеме листа и на листе 54; размеры — в мм по чистовым поверхностям; отметки — в м от ±0,000; высоты Н — от чистого пола помещения до оси изделия, у декора — до центра.
2. Красные цепочки — привязки электроточек и выводов: по горизонтали от угла чистовых стен, по вертикали от чистого пола, до оси изделия; звенья короче 3 мм на листе вынесены во второй ярус (ближняя к стене цепочка).
3. У знака электроточки: марка (Р — розетка, S — выключатель, Св — светильник, ЭВ — вывод кабеля), ×N — число постов в рамке, гр. — группа щита, Н — высота оси от чистого пола, мм; группы по клавишам выключателя — на листе выключателей.
4. Схема мебели, приборов и декора не является технической документацией для производства мебели; габариты — по паспортам изделий.
5. Картины и зеркала крепить к основанию по паспорту изделия (закладные и анкеры — в перечне скрытых работ); крест — ось центра предмета.
6. Карнизы (шины) — по ведомости текстиля декоратора; длина L и верх Н — по развёртке, крепление — до окраски потолка.

1000 мм · печать 1:1

Изм.	Кол.уч	Лист	№ док.	Подп.	Дата	ГД-2026-007-АИ			
						Квартира 65 м²			
						Общая площадь 65,24* м² · * размеры со скана, не замерены (реестр — п. 5, К-1)			
Разраб.		Кырпан А.С.			09.10.26	Дизайн-проект интерьера	Стадия	Лист	Листов
Пров.							РП	70	79
ГИП									
Н. контр.						Разверки стен А, Б. Детская (пом. 9)	Кырпан Александр Сергеевич		
Утв.						М 1:40			


выпуск 09.10.2026 № 147dabfd23 · стр. 81 из 110

Развёртки стен В, Г. Детская (пом. 9)

Детская (пом. 9) · вид изнутри помещения · размеры в мм, отметки в м

ПРЕДВАРИТЕЛЬНО · не для производства работ · открыто пунктов: 4 (реестр — л. 5)

Развёртка стены В

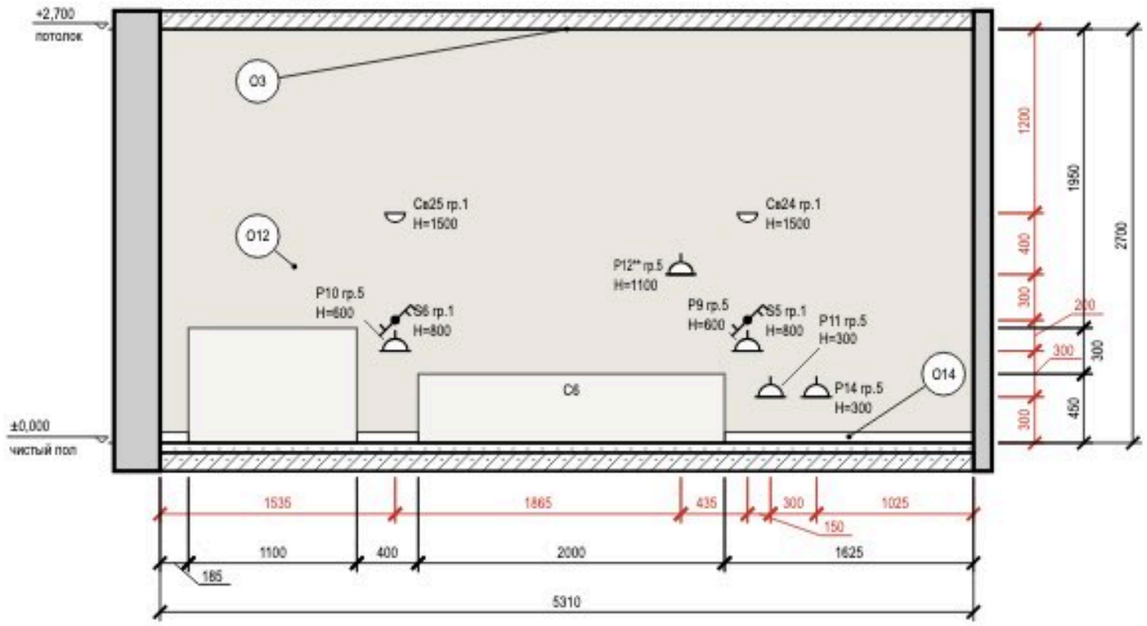

Развёртка стены Г


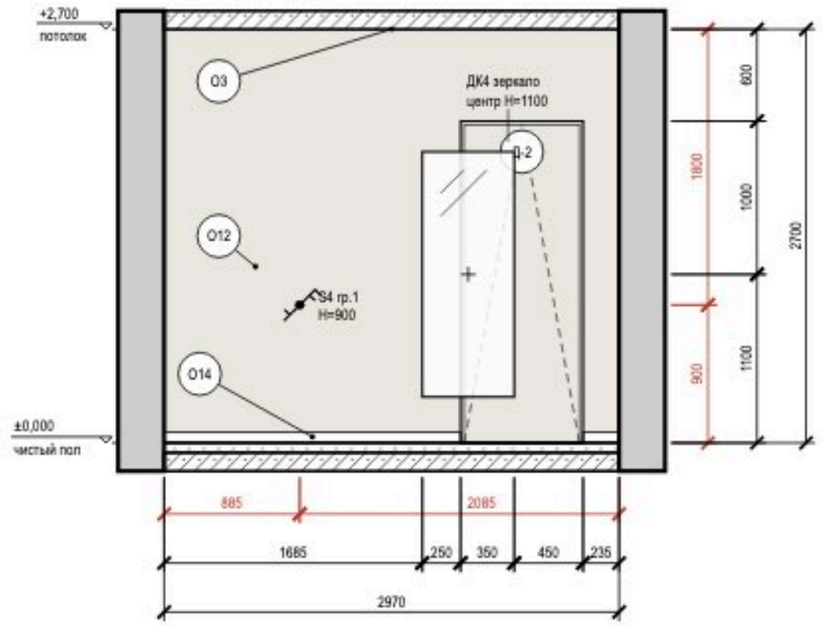


Схема развёрток (М 1:100)

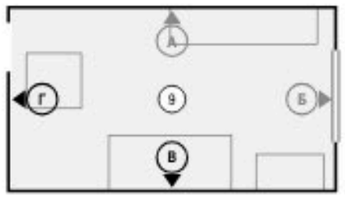

Условные обозначения

- розетка с заземляющим контактом; у знака — марка, ×N постов в рамке, гр. — группа щита, H — высота оси, мм
- выключатель одноклавишный
- выключатель двухклавишный (флажков — по числу клавиш)
- выключатель с проходной или перекрёстной клавишей (обратный флажок); тип клавиши — в подписи
- светильник настенный (бра), H — высота оси
- привязки точек и выводов от угла и от пола, мм
- мебель и приборы — фасад по расстановке (условно)
- зеркало: марка Д, крест — центр, H — высота центра, мм
- дверь скрытого монтажа: полотно в плоскости стены (узел — на листе узлов)
- стены и перекрытия в сечении
- окраска: тон — цвет по коду производителя (условно)
- О1 — марка отделки по реестру отделки альбома
- А — марка развёртки: буква стены, стрелка — взгляд

Ведомость отделки (на листе)

Марка	Поверхность	Материал, изделие	Цвет, код	Кол.
О3	потолок	окраска, Tikkurila Anti-Reflex 2, глубокоматовая, подготовка Q3	Tikkurila V503 «Winter»	16 м²
О12	стены	окраска, Farrow & Ball Modern Emulsion, матовая, подготовка Q3	Farrow & Ball No. 241 «Skimming Stone»	20,7 м²
О14	плинтус	плинтус МДФ, Orac Decor Contour (Luxeus), h 69 мм, SX165	Farrow & Ball No. 241 «Skimming Stone»	4,4 м

Допущения и предложения на листе

Основа листа: размеры сняты с растрового плана заказчика без размеров: масштаб восстановлен по площадям помещений (≈ 11,8 мм на пиксель), контрольный обмер не выполнен (К-1); высота потолка 2700 мм принята: на плане заказчика её нет (К-2); толщины стен 300 / 120 мм приняты по плану заказчика, не замерены (К-1); разрешённая мощность 15 кВт принята по типовым ТУ для квартиры, ТУ заказчиком не переданы (К-4).

Знак «**» — предложение проектировщика, заказчиком не утверждено (согласовать с заказчиком): записи в реестре нет: Р12 — высота 1100 мм выше нормы 1 м (ПУЭ 6.6.30) по назначению: питание ТВ над комодом, в одной зоне с выводами ТВ2 и LAN2.

См. лист открытых вопросов (лист 5, записи К-1, К-2, К-4).

Примечания

1. Развёртки — вид на стену изнутри помещения, по часовой стрелке; расположение — на схеме листа и на листе 54; размеры — в мм по чистовым поверхностям; отметки — в м от ±0,000; высоты H — от чистого пола помещения до оси изделия, у декора — до центра.
2. Красные цепочки — привязки электроточек и выводов: по горизонтали от угла чистовых стен, по вертикали от чистого пола, до оси изделия; звенья короче 3 мм на листе вынесены во второй ярус (ближняя к стене цепочка).
3. У знака электроточки: марка (Р — розетка, S — выключатель, Св — светильник, ЭВ — вывод кабеля), ×N — число постов в рамке, гр. — группа щита, H — высота оси от чистого пола, мм; группы по клавишам выключателя — на листе выключателей.
4. Схема мебели, приборов и декора не является технической документацией для производства мебели; габариты — по паспортам изделий.
5. Картины и зеркала крепить к основанию по паспорту изделия (закладные и анкеры — в перечне скрытых работ); крест — ось центра предмета.
6. Двери скрытого монтажа — полотно в плоскости стены, отделка стены по полотну, плинтус прерывается у короба (узел — на листе узлов).

1000 мм · печать 1:1

Изм.	Кол.уч	Лист	№ док.	Подп.	Дата
Разраб.		Кырпан А.С.			09.10.26
Пров.					
ГИП					
Н. контр.					
Утв.					

ГД-2026-007-АИ

Квартира 65 м²

Общая площадь 65,24* м² · * размеры со скана, не замерены (реестр — п. 5, К-1)

Дизайн-проект интерьера	Стадия	Лист	Листов
	РП	71	79
Развёртки стен В, Г. Детская (пом. 9) М 1:40	Кырпан Александр Сергеевич		


выпуск 09.10.2026 № 147dabfd23 · стр. 82 из 110

Узлы

Пороги и стыки покрытий, скрытые двери, короба стояков, гидроизоляция, плинтус


1 Порог 15 мм: мокрая зона — жилое помещение (М 1:5)

Применение: двери Д-4; места — лист 54

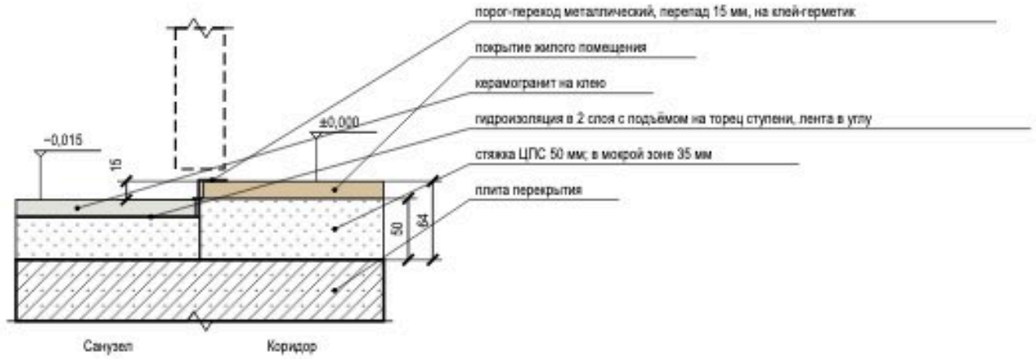


2 Дверь скрытого монтажа в плоскости стены, плинтус (М 1:5)

Применение: двери Д-3, Д-2, Д-4; места — лист 54

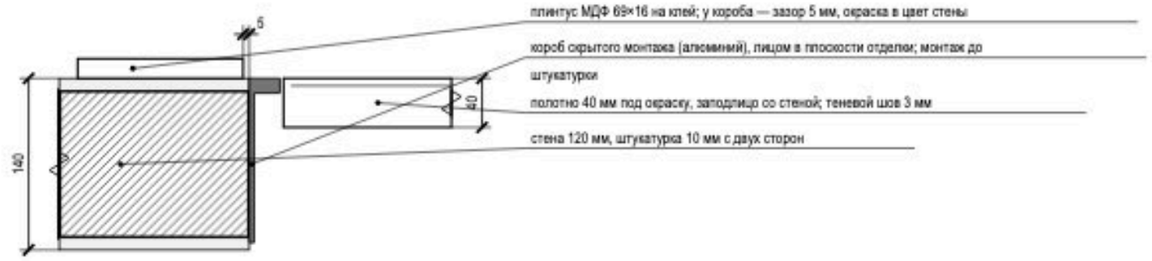


3 Короб стояков К1-1 с люком и звукоизоляцией (М 1:20)

Применение: пом. 6; места — лист 54

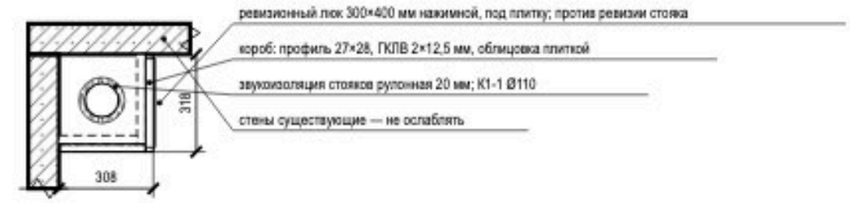


4 Гидроизоляция санузла: заход на стены 200 мм, примыкание ванны (М 1:20)

Применение: пом. 6, 7; места — лист 54

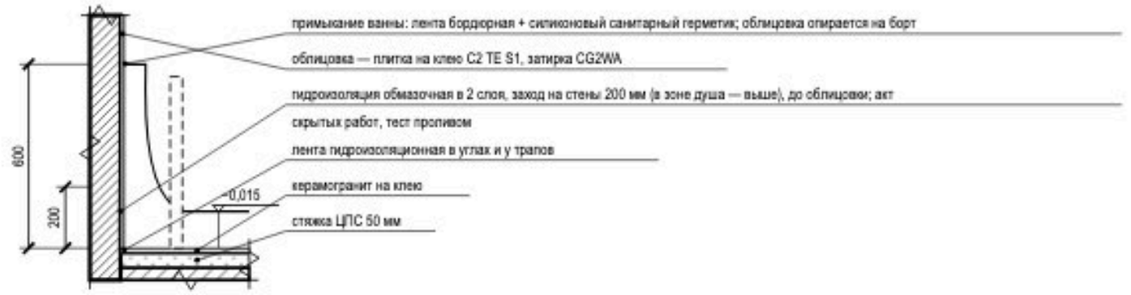

5 Плинтус МДФ 69×16 мм у окрашенной стены (М 1:10)

Применение: пом. 1, 2, 3, 4, 5, 8, 9; места — лист 54

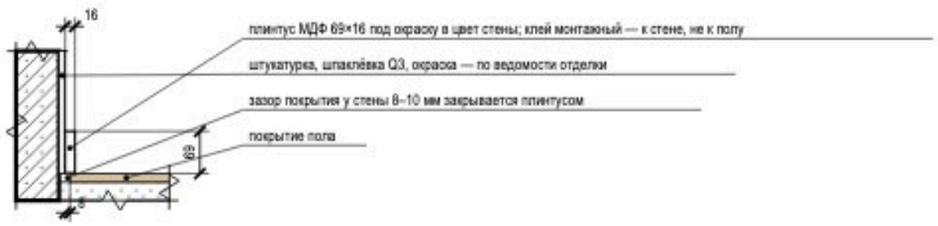

Условные обозначения

- железобетон (плита, стены)
- кладка, перегородка
- стяжка, раствор
- гипсокартон ГКЛВ
- звукоизоляция, эластичный заполнитель
- плитка, керамогранит на клею
- инженерная доска (покрытие пола)
- металлический профиль (порог, Т-профиль, короб двери)
- гидроизоляция (обмазочная, лента)

Примечания

1. Узлы — типовые решения проекта для мест, отмеченных выносками на листе схемы расположения развёрток и узлов; размеры — в мм, отметки — в м от ±0,000.
2. Узлы с гидроизоляцией, закладными и коробами скрытого монтажа принимаются по актам скрытых работ до закрытия отделкой; гидроизоляция — после теста проливом (24 ч).
3. Марки изделий (порог, Т-профиль, короб скрытой двери, люк) — по спецификациям; замена — на аналог с теми же габаритами по согласованию с автором проекта.

Допущения и предложения на листе

Основа листа: размеры сняты с растрового плана заказчика без размеров: масштаб восстановлен по площадям помещений (≈ 11,8 мм на пиксель), контрольный обмер не выполнен (К-1); высота потолка 2700 мм принята: на плане заказчика её нет (К-2); толщины стен 300 / 120 мм приняты по плану заказчика, не замерены (К-1); разрешённая мощность 15 кВт принята по типовым ТУ для квартиры, ТУ заказчиком не переданы (К-4).

См. лист открытых вопросов (лист 5, записи К-1, К-2, К-4).

Изм.	Кол.уч	Лист	№ док.	Подп.	Дата
Разраб.		Кырпан А.С.			09.10.26
Пров.					
ГИП					
Н. контр.					
Утв.					

ГД-2026-007-АИ

Квартира 65 м²

Общая площадь 65,24* м² · * размеры со скана, не замерены (реестр — п. 5, К-1)

Дизайн-проект интерьера

Стадия	Лист	Листов
РП	72	79

Узлы

М 6/м

Кырпан Александр Сергеевич

выпуск 09.10.2026 № 147dabfd23 · стр. 83 из 110

10

Смета

Кырлан Александр Сергеевич

выпуск 09.10.2026 № 147dabfd23 · стр. 84 из 110

Ведомость объёмов работ

ПРЕДВАРИТЕЛЬНО · не для производства работ · открыто пунктов: 4 (реестр — л. 5)

Объёмы по помещениям от чертежа · площади в м², длины в м · формула, правило проёмов и источник в каждой строке

Ведомость объёмов работ по помещениям

Поз.	Наименование работ (материал, число слоёв)	Ед. изм.	Объём по помещениям (№ по экспликации)									Всего	Формула подсчёта	Правило проёмов	Источник	Цена за ед., ₽	Стоимость, ₽
			1	2	3	4	5	6	7	8	9						
1. Демонтаж и черновые работы																	
1	Демонтаж существующего покрытия пола до основания	м²	4,20	8,27	18,91	4,15	5,51	1,83	3,85	2,50	16,02	65,24	S пом.		л. 11, 12	по КП	
2	Демонтаж существующей отделки стен до основания	м²	21,37	28,54	48,29	17,41	21,78	13,89	20,09	15,65	40,96	227,98	P × H − проёмы	за вычетом проёмов	л. 11, 12	по КП	
3	Демонтаж существующей отделки потолка до основания	м²	4,20	8,27	18,91	4,15	5,51	1,83	3,85	2,50	16,02	65,24	S пом.		л. 11, 12	по КП	
4	Демонтаж существующих дверных блоков	шт	1	1		1	5					8	по ведомости проёмов		л. 12, 13	по КП	
5	Демонтаж существующих сантехприборов и электрооборудования (если есть)	компл											по факту на объекте		л. 12	по КП	
6	Монтаж каркасной перегородки П-1: каркас ПС через 600 мм, ГКЛ в 2 слоя с каждой стороны	м²										4,72	1,75 × 2,70 = 4,72 м², одна сторона; пом.	проёмы вычтены	л. 12; схема каркаса перегородки	1 500	7 080
7	Заполнение каркаса П-1 минераловатной плитой (звукоизоляция, Rw — дБ)	м²										4,72	4,72 м² без проёма		схема каркаса перегородки	по КП	
8	Устройство стяжки: стяжка ЦПС М200, 50 мм	м²	4,24								16,07	20,31	S пом. + S в дверных проёмах (b × t/2)	проёмы добавлены	л. 34, 35	530	10 764
9	Гидроизоляция обмазочная, 2 слоя: пол, стены на 200 мм, зоны замачивания	м²						2,83	5,30			8,13	пол + (P − двери) × h заведения + зоны замачивания		л. 32	450	3 659
10	Штукатурка стен по маякам, до 10 мм	м²	21,37								40,96	62,33	P × H − проёмы по обводу коробок − грани перегородок на ГКЛВ	за вычетом проёмов	л. 11, 35	530	33 035
11	Штукатурка оконных откосов шириной более 200 мм	м²			1,86						1,08	2,94	Σ (2h + b) × глубина откоса	откосы > 200 мм	л. 11	540	1 588
Итого по разделу 1 — 56 126 ₽ (позиций 11, из них по КП 6); в сводную смету — л. 78, 79																	
2. Инженерные системы																	
12	Прокладка слаботочной линии: Кабель домофона — тип по системе поставщика, отдельно от силовых	м										3,10	по лучам от ЩС**: 1 точ., запас 10 %		л. 24	по КП	
13	Прокладка слаботочной линии: Кабель коаксиальный RG-6 (75 Ом) к розеткам ТВ, отдельно от силовых	м										30,20	по лучам от ЩС**: 2 точ., запас 10 %		л. 24	по КП	
14	Прокладка слаботочной линии: Кабель U/UTP кат. 5e (LAN, Wi-Fi и камеры по PoE), отдельно от силовых	м										42,70	по лучам от ЩС**: 3 точ., запас 10 %		л. 24	по КП	
15	Прокладка слаботочной линии: Кабель U/UTP кат. 6 (LAN, Wi-Fi и камеры по PoE), отдельно от силовых	м										14,20	по лучам от ЩС**: 1 точ., запас 10 %		л. 24	по КП	
16	Прокладка гофротрубы Ø20 для слаботочных линий, отдельно от силовых	м										81,20	по длине лучей без участков в канале плинтуса (≈ 90 %)		л. 24	по КП	
17	Сборка слаботочного щита ЩС**: корпус, патч-панель, подключение линий и питания 220 В; коммутатор и точки доступа — оборудование заказчика	шт										1	один щит		л. 21, 24	по КП	
18	Электроточка: подрозетник в бетоне, розетка, выключатель, вывод	шт		6	14	2	2		4		11	39	по ведомости электроточек		л. 18, 21	950	37 050
19	Штробы в стенах под спуски кабеля к точкам — выполняются только после технического заключения о несущих стенах	м		12,60	21,35	3,00	4,20		5,26		21,80	68,21	Σ (H − h) по точкам на стенах: вертикальные спуски	после техзаключения	л. 12, 18	по КП	
20	Установка встраиваемого точечного светильника	шт				1	2	1	1		6	11	по плану освещения		л. 19	750	8 250
21	Монтаж светильника: потолочного, подвесного, настенного	шт	1	4	4				1	1	2	13	по плану освещения		л. 19	1 200	15 600
22	Монтаж LED-ленты в алюминиевый профиль	м			2,50						12,30	14,80	Σ длин лент по плану освещения		л. 19	230	3 404

Допущения и предложения на листе

Основа листа: размеры сняты с растрового плана заказчика без размеров: масштаб восстановлен по площадям помещений (≈ 11,8 мм на пиксель), контрольный обмер не выполнен (К-1); высота потолка 2700 мм принята: на плане заказчика её нет (К-2); толщины стен 300 / 120 мм приняты по плану заказчика, не замерены (К-1); разрешённая мощность 15 кВт принята по типовым ТУ для квартиры, ТУ заказчиком не переданы (К-4).

Знак «**» — предложение проектировщика, заказчиком не утверждено (согласовать с заказчиком): записи в реестре нет: ЩС — щит слаботочный: место и состав.

См. лист открытых вопросов (лист 5, записи К-1, К-2, К-4).

Изм.	Кол.уч	Лист	№ док.	Подп.	Дата
Разраб.		Кырпан А.С.			09.10.26
Пров.					
ГИП					
Н. контр.					
Утв.					

ГД-2026-007-АИ

Квартира 65 м²

Общая площадь 65,24* м² · * размеры со скана, не замерены (реестр — л. 5, К-1)

Дизайн-проект интерьера

Стадия	Лист	Листов
РП	73	79

Ведомость объёмов работ

М 6/м

Кырпан Александр Сергеевич

выпуск 09.10.2026 · 147dabfd23 · стр. 85 из 110

Ведомость объёмов работ (продолжение)

Объёмы по помещениям от чертежа · площади в м², длины в м · формула, правило проёмов и источник в каждой строке

Ведомость объёмов работ по помещениям (продолжение)

Поз.	Наименование работ (материал, число слоёв)	Ед. изм.	Объём по помещениям (№ по экспликации)									Всего	Формула подсчёта	Правило проёмов	Источник	Цена за ед., ₽	Стоимость, ₽
			1	2	3	4	5	6	7	8	9						
23	Установка блока питания LED в доступном месте (люк, шкаф)	шт		1	1						1	3	один на LED-группу		л. 19	570	1 710
24	Установка автономного пожарного извещателя	шт		1	1						1	3	по плану розеток		л. 18	по КП	
25	Сборка щита: установка автоматов и АВДТ групп, вводного автомата	шт										6	группы + вводной автомат		л. 22	230	1 380
26	Установка вводного УЗО	шт										1	по однолинейной схеме		л. 22	380	380
27	Монтаж инсталляции, установка подвесного унитаза и кнопки смыва	шт						1				1	по плану выводов		л. 27, 29	10 500	10 500
28	Короб инсталляции: каркас и обшивка ГКЛВ в 2 слоя, ревизионный доступ к смыву	шт						1	1			2	по плану выводов		л. 27, 32, 33	по КП	
29	Короб К1 над чистым полом: каркас и обшивка ГКЛВ под плитку (материалы — в спецификации ВК)	м.п.						1,37	1,24			2,61	Σ открытых участков выпусков К1 (профиль листа разводки ВК)		л. 27, 29	по КП	
30	Установка ванны с сифоном	шт							1			1	по плану выводов		л. 27, 29	6 000	6 000
31	Установка умывальника (мойки) с сифоном и смесителем	шт			1			1	1			3	по плану выводов		л. 27, 29	3 000	9 000
32	Подключение стиральной (посудомоечной) машины к ВК	шт							1			1	по плану выводов		л. 27	по КП	
33	Установка радиатора с узлом подключения и терморегулятором	шт		1	1							2	по плану отопления		л. 26	по КП	
Итого по разделу 2 — 93 274 ₽ (позиций 22, из них по КП 12); в сводную смету — л. 78, 79																	
3. Чистовые работы																	
34	Облицовка стен керамической плитки 600×1200 на клею	м²						13,89	20,09			33,98	по раскладке: зона облицовки − место за коробом	за вычетом проёмов	л. 35	2 500	84 950
35	Укладка керамогранита на пол, 600×1200, на клею	м²				4,36	5,80	1,86	3,89			15,91	S пом. + S в дверных проёмах	проёмы добавлены	л. 32–34	1 800	28 638
36	Затирка швов керамогранита	м²				4,15	5,51	1,83	3,85			15,34	Σ S облицовки и пола из плитки		л. 32, 33	150	2 301
37	Грунтование стен, 2 слоя (под штукатурку и под отделку)	м²	21,37	28,54	48,29	17,41	21,78	13,89	20,09	15,65	40,96	227,98	P × H − проёмы	за вычетом проёмов	л. 35	96	21 886
38	Шпаклёвка стен под окраску, 2 слоя (старт и финиш), уровень Q3	м²	21,37	28,54	48,29	17,41	21,78			15,65	40,96	194,00	P × H − проёмы − фартук	за вычетом проёмов	л. 35	750	145 500
39	Грунтование и шпаклёвка оконных откосов, 2 слоя	м.п.			8,10						4,70	12,80	Σ (2h + b) по окнам	по окнам	л. 11	300	3 840
40	Грунтование потолка, 2 слоя	м²	4,20	8,27	18,91	4,15	5,51	1,83	3,85	2,50	16,02	65,24	S пом.		л. 35	96	6 263
41	Шпаклёвка потолка под окраску, 2 слоя, уровень Q3	м²	4,20	8,27	18,91	4,15	5,51	1,83	3,85	2,50	16,02	65,24	S пом.		л. 31, 35	950	61 978
42	Окраска потолка водно-дисперсионной краской, 2 слоя	м²	4,20	8,27	18,91	4,15	5,51	1,83	3,85	2,50	16,02	65,24	S пом.		л. 35	360	23 486
43	Окраска стен водно-дисперсионной краской, 2 слоя	м²	22,84	31,48	54,16	22,03	31,97			17,12	45,04	224,64	P × H − фартук, проёмы не вычитаются	без вычета проёмов	л. 35	300	67 392
44	Окраска оконных откосов, 2 слоя	м.п.			8,10						4,70	12,80	Σ (2h + b) по окнам	по окнам	л. 11	120	1 536
45	Укладка инженерной доски на клей	м²	4,24	8,35	19,00					2,54	16,07	50,20	S пом. + S в дверных проёмах	проёмы добавлены	л. 34, 35	1 200	60 240
46	Установка плинтуса МДФ h=69 мм	м.п.	7,76	10,26	18,56	5,96	6,99			5,64	15,88	71,05	P − ширина дверных проёмов		л. 35	450	31 973
47	Окраска плинтуса в тон V503, 2 слоя	м.п.	7,76	10,26	18,56	5,96	6,99			5,64	15,88	71,05	как плинтус		л. 35	300	21 315
48	Монтаж дверей скрытого монтажа под покраску (поставщик дверей)	шт	1	1			5					7	по ведомости проёмов		л. 13	5 250	36 750
49	Входная дверь, поставка с монтажом и откосами	шт										1	по ведомости проёмов		л. 13	по КП	
Итого по разделу 3 — 598 048 ₽ (позиций 16, из них по КП 1); в сводную смету — л. 78, 79																	

Допущения и предложения на листе

Основа листа: размеры сняты с растрового плана заказчика без размеров: масштаб восстановлен по площадям помещений (≈ 11,8 мм на пиксель), контрольный обмер не выполнен (К-1); высота потолка 2700 мм принята: на плане заказчика её нет (К-2); толщины стен 300 / 120 мм приняты по плану заказчика, не замерены (К-1); разрешённая мощность 15 кВт принята по типовым ТУ для квартиры, ТУ заказчиком не переданы (К-4).

См. лист открытых вопросов (лист 5, записи К-1, К-2, К-4).

Изм.	Кол.уч	Лист	№ док.	Подп.	Дата
Разраб.		Кырпан А.С.			09.10.26
Пров.					
ГИП					
Н. контр.					
Утв.					

ГД-2026-007-АИ

Квартира 65 м²

Общая площадь 65,24* м² · * размеры со скана, не замерены (реестр — л. 5, К-1)

Дизайн-проект интерьера	Стадия	Лист	Листов
	РП	74	79
Ведомость объёмов работ (продолжение) М 6\м	**Кырпан Александр Сергеевич**		

выпуск 09.10.2026 · 147dabfd23 · стр. 86 из 110

Ведомость объёмов работ (окончание)

Объёмы по помещениям от чертежа · площади в м², длины в м · формула, правило проёмов и источник в каждой строке

Ведомость подсчёта площадей по помещениям

№	Помещение	S пола, м²	P, м	H, м	P × H, м²	Проёмы, м²	Стены нетто, м²	В дверных проёмах, м²	Плинтус, м	Откосы, м.п.
1	Гардеробная	4,20	8,46	2,70	22,84	1,47	21,37	0,04	7,76	нет
2	Спальня	8,27	11,66	2,70	31,48	2,94	28,54	0,08	10,26	нет
3	Кухня-гостиная	18,91	20,06	2,70	54,16	5,87	48,29	0,09	18,56	8,10
4	Прихожая	4,15	8,16	2,70	22,03	4,62	17,41	0,21	5,96	нет
5	Коридор	5,51	11,84	2,70	31,97	10,19	21,78	0,29	6,99	нет
6	Санузел	1,83	5,54	2,71	15,04	1,16	13,89	0,03	нет	нет
7	Ванная	3,85	7,94	2,71	21,56	1,47	20,09	0,04	нет	нет
8	Кладовая	2,50	6,34	2,70	17,12	1,47	15,65	0,04	5,64	нет
9	Детская	16,02	16,68	2,70	45,04	4,08	40,96	0,05	15,88	4,70
	Итого	**65,24**			**261,24**	**33,26**	**227,98**	**0,89**	**71,05**	**12,80**

Реестр контрольных сумм

Показатель	По ВОР	По чертежу	Расхождение	Лист
Σ площадей помещений без летних, м² — общая площадь по экспликации	65,24	65,24	0,0 %	л. 11
Стены под окраску, м² (шпаклёвка) ведомость отделки	194,00	194,00	0,0 %	л. 35
Потолки под окраску, м² — ведомость отделки	65,24	65,24	0,0 %	л. 35
Плинтус, м — ведомость отделки	71,05	71,05	0,0 %	л. 35
Плитка к заказу, шт — ведомость плитки	32	32	0,0 %	л. 32
Точки ЭОМ, шт — планы ЭОМ (без щитов)	71	72	-1,4 %	л. 18, 19

Примечания

1. Объёмы — от геометрии проекта (та же, что на планах и в ведомости отделки), не от общей площади: P — периметр чистого контура, H — от чистого пола до низа потолка, проёмы — по наружному обводу коробок.
2. Подсчёт по ГЭСН-2001-15 и ГЭСН-2001-11: штукатурка и шпаклёвка стен — за вычетом проёмов; окраска водными составами — без вычета проёмов (п. 2.24); откосы — отдельно, по ширине до 200 и более 200 мм; полы — с площадью в дверных проёмах.
3. Плитка — по раскладке (целые и с подрезкой); короб инсталляции и фартук — отдельными строками, двойного счёта облицовки нет. Материалы, запас и количество к заказу — в спецификации материалов.
4. Цены — ориентир по открытым прайсам Москвы (прайсы собраны 21.09.2026, часть расценок сверена повторно 06.10.2026), не коммерческое предложение; «по КП» — расценки нет, строка в итог не входит.
5. Демонтаж — по плану демонтажа и общим указаниям: покрытия пола, отделка стен и потолков, дверные блоки — до основания; объёмы справочные, уточняются по факту на объекте (расценки в книге нет — «по КП»).
6. Штробы в стенах — только после технического заключения о несущих стенах (общие указания, план обмера и демонтажа): строка «Штробы в стенах» вертикальные спуски кабеля от потолочной трассы к точкам, объём не меньше фактического (горизонтальные трассы — по исполнительной схеме). Расценки штробления в прайсе нет — «по КП», в итог не входит; кабель в штробах стен прокладывается после неё.
7. Слаботочные сети: кабель по лучам от ЩС** 90,20 м (U/UTP, RG-6, домофон — по видам), гофра 81,20 м, щит ЩС** с патч-панелью; розетки RJ45 и ТВ монтируются в строке «Электроточка». Длины те же, что в ведомости изделий электрика (одна модель — lowcurrent-engineer/bom.js); оборудование заказчика (точки доступа, камеры, коммутатор) в спецификацию не входит.
8. Перегородки и облицовки ГКЛ (П-1 — 4,72 м²): площадь одной стороны за вычетом проёмов, из той же модели, по которой выпущена схема каркаса; обшивка, профиль и заполнение — в спецификации материалов. Грани перегородок на ГКЛВ вычтены из штукатурки стен (0,00 м²): штукатурят основание, а не обшивку.
9. Коробы: стояков (нет) и К1 над чистым полом (2,61 м открытых участков; труба К1 вдоль стен 14,18 м в короб не зашивается — она за приборами, в раме инсталляции и в шахтах). В спецификации ВК короб К1 заказывается с запасом 10 % — 2,90 м. Материалы коробов стояков и инсталляции — в спецификации материалов, К1 — в спецификации ВК.

Допущения и предложения на листе

Основа листа: размеры сняты с растрового плана заказчика без размеров: масштаб восстановлен по площадям помещений (≈ 11,8 мм на пиксель), контрольный обмер не выполнен (К-1); высота потолка 2700 мм принята: на плане заказчика её нет (К-2); толщины стен 300 / 120 мм приняты по плану заказчика, не замерены (К-1); разрешённая мощность 15 кВт принята по типовым ТУ для квартиры, ТУ заказчиком не переданы (К-4).

Знак «**» — предложение проектировщика, заказчиком не утверждено (согласовать с заказчиком): записи в реестре нет: ЩС — щит слаботочный: место и состав.

См. лист открытых вопросов (лист 5, записи К-1, К-2, К-4).

Изм.	Кол.уч	Лист	№ док.	Подп.	Дата	ГД-2026-007-АИ			
						Квартира 65 м²			
						Общая площадь 65,24* м² · * размеры со скана, не замерены (реестр — л. 5, К-1)			
Разраб.		Кырпан А.С.			09.10.26	Дизайн-проект интерьера	Стадия	Лист	Листов
Пров.							РП	75	79
ГИП									
Н. контр.						Ведомость объёмов работ (окончание)	Кырпан Александр Сергеевич		
Утв.						М 6/м			

выпуск 09.10.2026 · 147dabfd23 · стр. 87 из 110

Спецификация материалов

Отделочные материалы: чистое количество, запас, упаковка, к заказу · ГОСТ 21.110-2013

Спецификация материалов (ГОСТ 21.110-2013, форма 1)

Поз.	Наименование и техническая характеристика	Тип, марка, артикул	Код продукции	Поставщик	Ед. изм.	Количество				Масса ед., кг	Примечание
						чистое	запас, %	упаковка	к заказу		
Покрытия полов и облицовка											
1	Инженерная доска (дуб натуральный, рабочий слой 4 мм, эмиссия E1, прямая укладка)	IM1848			м²	50,21	7	по артикулу	53,80 м²		пом. 1, 2, 3, 8, 9; до целой упаковки; л. 34, 35
2	Клей для паркетной и инженерной доски (эластичный, по ТУ изготовителя доски)	по выбору подрядчика			м²	50,21		ведро по ТУ	по ТУ		расход кг/м² — по ТУ клея; л. 34
3	Керамогранит 600×1200 мм SG501600R	SG501600R			шт	28	10	коробка	32 шт		0 целых + 28 с подрезкой; 15,34 м² по раскладке, к заказу 23,04 м²; пом. 4, 5, 6, 7; л. 32, 33
4	Керамическая плитка 600×1200 мм	610010001195			м²	33,97	10	коробка	37,40 м²		пом. 6 (стены), 7 (стены); раскладки нет — по площади отделки; л. 35
Сухие смеси и гидроизоляция											
5	Клей плиточный цементный класса C2 (ГОСТ Р 56387-2018)	по выбору подрядчика			кг	71,12	10	мешок 25 кг	4 меш.	25	слой 5 мм, 1,50 кг/м² на 1 мм; л. 32
6	Клей плиточный цементный класса C2 S1 (ГОСТ Р 56387-2018)	по выбору подрядчика			кг	41,09	10	мешок 25 кг	2 меш.	25	слой 5 мм, 1,50 кг/м² на 1 мм; л. 32
7	Затирка цементная класса класс не задан, цвет — по колерной карте	по выбору подрядчика			кг	1,08	10	упак. 2 кг	1 упак.	2	расход (a+b)/ab × шов × t × 1,6 кг/м²; л. 32
8	Гидроизоляция обмазочная полимерная, 2 слоя, лента в углах, манжеты на выводах	по выбору подрядчика			м²	8,13	10	ведро по ТУ	по ТУ		пом. 6, 7; расход кг/м² — по ТУ; л. 32
9	Лента демпферная по периметру пола из плитки	по выбору подрядчика			м	24,70	10	рулон	28,00 м		л. 32
10	Смесь цементно-песчаная для стяжки М200 (50 мм)	по выбору подрядчика			м³	1,02	5	мешок по ТУ	по ТУ		S 20,31 м² × толщина; армирование и маяки — по ТУ; л. 34
11	Смесь штукатурная гипсовая для машинного и ручного нанесения по маякам, слой до 10 мм	по выбору подрядчика			м²	62,33	10	мешок по ТУ	по ТУ		пом. 1, 9; расход кг/м² на 1 мм слоя — по ТУ смеси, толщина — по замеру кривизны стен; л. 11, 35
Перегородки и облицовки из ГКЛВ											
12	Лист ГКЛ 12,5 мм, 2500 × 1200 мм: обшивка перегородок и облицовок, 2 слоя на сторону	по выбору подрядчика			м²	18,88	10	лист 3,00 м²	7,00 лист		П-1; площадь стороны × 2 слоя × стороны (проёмы вычтены); л. 12; схема каркаса перегородки
13	Профиль направляющий ПН 100: по потолку и полу, перемычки над проёмами	по выбору подрядчика			м	3,50	10	хлыст 3 м	2 шт		П-1; ПН: шаг и положение стоек — на схеме каркаса; длина стойки равна высоте перегородки, стойки режут между направляющими при монтаже; л. 12; схема каркаса перегородки
14	Профиль стоечный ПС 100: стойки через шаг каркаса и короткие над проёмами	по выбору подрядчика			м	10,80	10	хлыст 3 м	4 шт		П-1; ПС: шаг и положение стоек — на схеме каркаса; длина стойки равна высоте перегородки, стойки режут между направляющими при монтаже; л. 12; схема каркаса перегородки
15	Плита минераловатная звукопоглощающая в полость каркаса, толщина по глубине профиля 100 мм	по выбору подрядчика			м²	4,72	10	упаковка по ТУ	по ТУ		П-1; заполнение принято (К-18): марка и плотность — при закупке; Rw системы нормируют с заполнением; л. 12; схема каркаса перегородки
16	Лента уплотнительная самоклеящаяся под профили по потолку, полу и у примыканий к стенам	по выбору подрядчика			м	3,50	10	рулон по ТУ	4,00 м		П-1; по периметру каркаса: потолок, пол без проёма, крайние стойки у примыканий; л. 12; схема каркаса перегородки
17	Саморезы для ГКЛ по металлу (по слоям обшивки), дюбели для направляющих — по ТУ изготовителя системы	по выбору подрядчика			м²	18,88		упаковка по ТУ	по ТУ		П-1; расход шт/м² и шаг дюбелей — по ТУ системы; считаются от площади обшивки; л. 12; схема каркаса перегородки
Слаботочные сети											
18	Кабель домофона — тип по системе поставщика	по выбору подрядчика			м	3,10		бухта по ТУ	4,00 м		по лучам от ЩС**, 1 точ., запас 10 % уже в длине; л. 24
19	Кабель коаксиальный RG-6 (75 Ом) к розеткам ТВ	по выбору подрядчика			м	30,20		бухта по ТУ	31,00 м		по лучам от ЩС**, 2 точ., запас 10 % уже в длине; л. 24
20	Кабель U/UTP кат. 5e (LAN, Wi-Fi и камеры по PoE)	по выбору подрядчика			м	42,70		бухта по ТУ	43,00 м		по лучам от ЩС**, 3 точ., запас 10 % уже в длине; л. 24

Допущения и предложения на листе

Основа листа: размеры сняты с растрового плана заказчика без размеров: масштаб восстановлен по площадям помещений (≈ 11,8 мм на писсель), контрольный обмер не выполнен (К-1); высота потолка 2700 мм принята: на плане заказчика её нет (К-2); толщины стен 300 / 120 мм приняты по плану заказчика, не замерены (К-1); разрешённая мощность 15 кВт принята по типовым ТУ для квартиры, ТУ заказчиком не переданы (К-4).

Знак «**» — предложение проектировщика, заказчиком не утверждено (согласовать с заказчиком): записи в реестре нет: ЩС — щит слаботочный: место и состав.

См. лист открытых вопросов (лист 5, записи К-1, К-2, К-4).

Изм.	Кол.уч	Лист	№ док.	Подп.	Дата
Разраб.		Кырпан А.С.			09.10.26
Пров.					
ГИП					
Н. контр.					
Утв.					

ГД-2026-007-АИ

Квартира 65 м²

Общая площадь 65,24* м² · * размеры со скана, не замерены (реестр — л. 5, К-1)

Дизайн-проект интерьера

Стадия	Лист	Листов
РП	76	79

Спецификация материалов

М 6/м

Кырпан Александр Сергеевич

выпуск 09.10.2026 · 147dabfd23 · стр. 88 из 110

Спецификация материалов (окончание)

Отделочные материалы: чистое количество, запас, упаковка, к заказу · ГОСТ 21.110-2013

Спецификация материалов (ГОСТ 21.110-2013, форма 1) (продолжение)

Поз.	Наименование и техническая характеристика	Тип, марка, артикул	Код продукции	Поставщик	Ед. изм.	Количество				Масса ед., кг	Примечание
						чистое	запас, %	упаковка	к заказу		
21	Кабель U/UTP кат. 6 (LAN, Wi-Fi и камеры по PoE)	по выбору подрядчика			м	14,20		бухта по ТУ	15,00 м		по лучам от ЩС**, 1 точ., запас 10 % уже в длине; л. 24
22	Гофротруба Ø20 для слаботочных линий, отдельно от силовых	по выбору подрядчика			м	81,20		бухта по ТУ	82,00 м		по длине лучей без участков в канале плинтуса (≈ 90 %); л. 24
23	Розетка компьютерная RJ45, кат. 6, с рамкой и подрозетником	по выбору подрядчика			шт	4		шт	4 шт		LAN1, LAN2; серия механизмов — как у розеток и выключателей; л. 21, 24
24	Розетка телевизионная (коаксиальная) с рамкой и подрозетником	по выбору подрядчика			шт	2		шт	2 шт		ТВ1, ТВ2; серия механизмов — как у розеток и выключателей; л. 21, 24
25	Трубка или монитор домофона (поставка домофонной организации)	по выбору подрядчика			шт	1		шт	1 шт		ДФ1; серия механизмов — как у розеток и выключателей; л. 21, 24
26	Щит слаботочный ЩС**: корпус, DIN-рейка, розетки 220 В	по выбору подрядчика			шт	1		шт	1 шт		ЩС**; серия механизмов — как у розеток и выключателей; л. 21, 24
27	Патч-панель, портов не менее 4	по выбору подрядчика			шт	1		шт	1 шт		серия механизмов — как у розеток и выключателей; л. 21, 24
Лакокрасочные материалы											
28	Краска интерьерная акриловая, матовая, класс истирания 1	Tikkurila Harmony V503 «Winter»			л	5,13	10	банка 2,7 л	3 банк		21,37 м² × 2 сл. × 0,12 л/м²; пом. 1; л. 35
29	Краска интерьерная акриловая, глубокоматовая, класс истирания 2	Tikkurila Anti-Reflex 2 V503 «Winter»			л	4,85	10	банка 2,7 л	2 банк		20,22 м² × 2 сл. × 0,12 л/м²; пом. 1 (пот.), 9 (пот.); л. 35
30	Краска интерьерная акриловая, глубокоматовая, класс истирания 2	Tikkurila S 1502-Y50R			л	6,85	10	банка 2,7 л	3 банк		28,54 м² × 2 сл. × 0,12 л/м²; пом. 2; л. 35
31	Краска интерьерная водно-дисперсионная, глубокоматовая, класс истирания 2	Tikkurila S 0300-N			л	10,80	10	банка 2,7 л	5 банк		45,02 м² × 2 сл. × 0,12 л/м²; пом. 2 (пот.), 3 (пот.), 4 (пот.), 5 (пот.), 6 (пот.), 7 (пот.), 8 (пот.); л. 35
32	Краска интерьерная акриловая, полуматовая, класс истирания 1	Tikkurila S 1002-Y50R			л	11,59	10	банка 2,7 л	5 банк		48,29 м² × 2 сл. × 0,12 л/м²; пом. 3; л. 35
33	Краска интерьерная акриловая, полуматовая, класс истирания 1	Tikkurila S 1502-Y50R			л	9,41	10	банка 2,7 л	4 банк		39,19 м² × 2 сл. × 0,12 л/м²; пом. 4, 5; л. 35
34	Краска интерьерная акриловая, матовая, класс истирания 2	Tikkurila S 0502-Y			л	3,76	10	банка 2,7 л	2 банк		15,65 м² × 2 сл. × 0,12 л/м²; пом. 8; л. 35
35	Краска интерьерная акриловая, матовая, класс истирания 1	Farrow & Ball Modern Emulsion No. 30 «Hague Blue»			л	3,46	10	банка 2,5 л	2 банк		14,42 м² × 2 сл. × 0,12 л/м²; пом. 9; л. 35
36	Краска интерьерная акриловая, матовая, класс истирания 1	Farrow & Ball Modern Emulsion No. 241 «Skimming Stone»			л	6,37	10	банка 2,5 л	3 банк		26,54 м² × 2 сл. × 0,12 л/м²; пом. 9; л. 35
37	Шпаклёвка финишная полимерная под окраску (стены и потолки, Q3)	по выбору подрядчика			м²	259,24	10	ведро по ТУ	по ТУ		расход кг/м² на слой — по ТУ; л. 35
38	Грунтовка акриловая глубокого проникновения, 2 слоя	по выбору подрядчика			м²	293,22	10	канистра по ТУ	по ТУ		расход л/м² — по ТУ; л. 35
Погонажные изделия и потолки											
39	Плинтус напольный МДФ под покраску, h=69 мм, крепление к стене	SX165			м.п.	71,05	10	хлыст 2,4 м	33 шт		пом. 1, 2, 3, 4, 5, 8, 9; длина хлыста — по артикулу; л. 35

Примечания

1. Чистое количество — из ведомости объёмов работ и раскладки плитки; запас — отдельной графой (доска — по ведомости отделки, плитка, краска и плинтус — 10 %); «к заказу» — с запасом и кратно упаковке.
2. Плитка — штуками по раскладке, запас на каждую поверхность. Калибр (рабочий размер) и тон — одной партией на помещение, калибр указать при заказе и сверить с раскладкой до укладки.
3. Краска — 0,12 л/м² на слой (середина вилки 0,10–0,15 л/м²) по фактической площади окраски из ведомости отделок; колеровка одной партией.
4. «По ТУ» — расход задаёт производитель выбранного продукта; количество к заказу — после выбора марки.
5. Штукатурная смесь — на ту же площадь, что строка ВОР «Штукатурка стен» (62,33 м²): площадь одна, расход смеси задаёт производитель.
6. Потолки ГКЛ: в этой спецификации — площадь системы П113; число листов, профилей и подвесов — по шагам каркаса на листе потолков (подвесы через 1000, несущие через 500, основные через 1200 мм), схема каркаса не вытущена. Сантехника, светильники и мебель — по своим спецификациям.

Допущения и предложения на листе

Основа листа: размеры сняты с растрового плана заказчика без размеров: масштаб восстановлен по площадям помещений (≈ 11,8 мм на пиксель), контрольный обмер не выполнен (К-1); высота потолка 2700 мм принята: на плане заказчика её нет (К-2); толщины стен 300 / 120 мм приняты по плану заказчика, не замерены (К-1); разрешённая мощность 15 кВт принята по типовым ТУ для квартиры, ТУ заказчиком не переданы (К-4).

Знак «**» — предложение проектировщика, заказчиком не утверждено (согласовать с заказчиком): записи в реестре нет: ЩС — щит слаботочный: место и состав.

См. лист открытых вопросов (лист 5, записи К-1, К-2, К-4).

Изм.	Кол.уч	Лист	№ док.	Подп.	Дата
Разраб.		Кырпан А.С.			09.10.26
Пров.					
ГИП					
Н. контр.					
Утв.					

ГД-2026-007-АИ

Квартира 65 м²

Общая площадь 65,24* м² · * размеры со скана, не замерены (реестр — л. 5, К-1)

Дизайн-проект интерьера	Стадия	Лист	Листов
	РП	77	79
Спецификация материалов (окончание) М 6/м	**Кырпан Александр Сергеевич**		

Смета ориентировочная

ПРЕДВАРИТЕЛЬНО · не для производства работ · открыто пунктов: 4 (реестр — л. 5)

Работы, материалы, оборудование, услуги и резерв · цены — ориентир по открытым прайсам, не коммерческое предложение

Сводная смета (прайсы собраны 21.09.2026, часть расценок сверена повторно 06.10.2026, Москва)

№	Наименование работ, материалов, услуг	Ед. изм.	Кол-во	Цена за ед., ₽	Стоимость, ₽			Чей подряд	Срок поставки, дн.	Основание	Источник цены
					план	факт	разница				
Работы — по ведомости объёмов работ											
1	Демонтаж и черновые работы (без 6 поз. по КП)	раздел	1		56 126			бригада		ВОР, поз. 1–11; л. 73–75	по ВОР
2	Инженерные системы (без 12 поз. по КП)	раздел	1		93 274			бригада		ВОР, поз. 12–33; л. 73–75	по ВОР
3	Чистовые работы (без 1 поз. по КП)	раздел	1		598 048			бригада, поставщик		ВОР, поз. 34–49; л. 73–75	по ВОР
Материалы — по спецификации материалов											
4	Инженерная доска	м²	53,80	4 513	242 799			поставщик		спецификация, поз. 1	Ц7
5	Керамогранит 600×1200 мм	м²	60,44	3 500	211 540			поставщик		спецификация, поз. 3, 4	Ц6
6	Клей плиточный цементный класса С2	меш.	6	1 800	10 800			поставщик		спецификация, поз. 5, 6	Ц7
7	Краска Tikkurila (Harmony, Anti-Reflex 2), банка 2,7 л	банк	24	3 510	84 240			поставщик		спецификация, поз. 28, 29, 30, 31, 32, 33, 34	Ц6
8	Краска Farrow & Ball Modern Emulsion, банка 2,5 л	банк	5	5 800	29 000			поставщик		спецификация, поз. 35, 36	Ц7
9	Плинтус напольный МДФ под покраску	шт	33	368	12 144			поставщик		спецификация, поз. 39	Ц7
10	Прочие материалы с расходом по ТУ (клей для доски, затирка, гидроизоляция, демпферная лента, смесь для стяжки, смесь штукатурная гипсовая для машинного и ручного нанесения по маякам, ГКЛВ перегородок, профиль ПН, профиль ПС, минвата в каркас, лента уплотнительная, крепёж каркаса, кабель слаботочки, гофра слаботочки, изделия слаботочки, шпаклёвка, грунтовка)	компл	1	по КП				поставщик		спецификация, поз. 2, 7, 8, 9, 10, 11, 12, 13, 14, 15, 16, 17, 18, 19, 20, 21, 22, 23, 24, 25, 26, 27, 37, 38	
Оборудование и мебель — поставка по спецификациям											
11	Кухонный гарнитур по проекту кухни, изготовление и монтаж (4–8 нед.)	компл	1	по КП				поставщик	уточн.; ориентир 4–8 нед. от замера	л. 49, 50	
12	Двери скрытого монтажа с коробом под покраску, поставка	шт	7	по КП				поставщик	уточн.; ориентир ≈ 30 дн.	л. 13	

Допущения и предложения на листе

Основа листа: размеры сняты с растрового плана заказчика без размеров: масштаб восстановлен по площадям помещений (≈ 11,8 мм на пиксель), контрольный обмер не выполнен (К-1); высота потолка 2700 мм принята: на плане заказчика её нет (К-2); толщины стен 300 / 120 мм приняты по плану заказчика, не замерены (К-1); разрешённая мощность 15 кВт принята по типовым ТУ для квартиры, ТУ заказчиком не переданы (К-4).

См. лист открытых вопросов (лист 5, записи К-1, К-2, К-4).

Изм.	Кол.уч	Лист	№ док.	Подп.	Дата
Разраб.		Кырпан А.С.			09.10.26
Пров.					
ГИП					
Н. контр.					
Утв.					

ГД-2026-007-АИ

Квартира 65 м²

Общая площадь 65,24* м² · * размеры со скана, не замерены (реестр — п. 5, К-1)

Дизайн-проект интерьера	Стадия	Лист	Листов
	РП	78	79

Смета ориентировочная

М 6/м

Кырпан Александр Сергеевич

выпуск 09.10.2026 № 147dabfd23 · стр. 90 из 110

Смета ориентировочная (окончание)

Работы, материалы, оборудование, услуги и резерв · цены — ориентир по открытым прайсам, не коммерческое предложение

Сводная смета (прайсы собраны 21.09.2026, часть расценок сверена повторно 06.10.2026, Москва) (продолжение)

№	Наименование работ, материалов, услуг	Ед. изм.	Кол-во	Цена за ед., ₽	Стоимость, ₽			Чей подряд	Срок поставки, дн.	Основание	Источник цены
					план	факт	разница				
13	Оборудование заказчика слаботочных сетей: коммутатор — 1 шт	компл	1	по КП				заказчик		л. 21	
14	Сантехника, светильники, мебель и предметы интерьера	компл	1	по КП				поставщик		л. 29; л. 30; л. 52; л. 16, 17	
Прочие работы и услуги											
15	Вынос и вывоз строительного мусора	м³		по факту				бригада		после демонтажа	
16	Подъём материалов на этаж (лифтом или вручную — по договору)	т		по факту				бригада		по массе поставки	
17	Доставка чистовых материалов, 10 % от поставки			10 %	59 052			поставщик		от суммы материалов	
18	Уборка после ремонта	м²	65,24	по факту				бригада		S квартиры	
	Итого работы				**747 448**						
	Итого материалы				**590 523**						
	Итого прочие услуги				**59 052**						
	Резерв на непредвиденные работы и материалы, 15 %				**209 553**						
	ВСЕГО ориентировочно (без оборудования и позиций по КП)				**1 606 576**						

Примечания

1. Смета ориентировочная, не коммерческое предложение: объёмы — из ведомости объёмов работ и спецификации материалов, цены — нижняя граница открытых прайсов Москвы (прайсы собраны 21.09.2026, часть расценок сверена повторно 06.10.2026); перед договором цены подтвердить у подрядчика и поставщиков.
2. Источники цен: Ц1 — Домашний мастерок: прайс на отделочные работы, 2026; Ц2 — Домашний мастерок: прайс на плиточные работы, 2026; Ц3 Домашний мастерок: прайс на электромонтажные работы, 2026; Ц4 — Профи ремонтник: штукатурно-малярные работы; Ц5 — Profi.ru: укладка керамогранита на стены, Москва 2026; Ц6 — knowledge/spec-materials.md, разд. 1 и 3: ориентир по сегментам; Ц7 — Розница Москвы, 09.2026: Леманa ПРО, KGSnab, официальный дилер Farrow & Ball.
3. Повторная сверка с прайсом: 06.10.2026 — перегородка в 2 слоя; остальные расценки — по прайсам, собранным 21.09.2026.
4. В итог не вошли позиции «по КП» и «по факту»: оборудование и мебель, двери, материалы с расходом по ТУ, вывоз мусора, подъём и уборка.
5. Доставка — 10 % от материалов, резерв — 15 % (частный ремонт 10–20 %) отдельными строками, в количествах не спрятаны. Графы «факт» и «разница» заполняются по актам.

Допущения и предложения на листе

Основа листа: размеры сняты с растрового плана заказчика без размеров: масштаб восстановлен по площадям помещений (≈ 11,8 мм на пиксель), контрольный обмер не выполнен (К-1); высота потолка 2700 мм принята: на плане заказчика её нет (К-2); толщины стен 300 / 120 мм приняты по плану заказчика, не замерены (К-1); разрешённая мощность 15 кВт принята по типовым ТУ для квартиры, ТУ заказчиком не переданы (К-4).

См. лист открытых вопросов (лист 5, записи К-1, К-2, К-4).

						ГД-2026-007-АИ
						Квартира 65 м²
Изм.	Кол.уч	Лист	№ док.	Подп.	Дата	Общая площадь 65,24* м² · * размеры со скана, не замерены (реестр — п. 5, К-1)
Разраб.		Кырпан А.С.			09.10.26	Дизайн-проект интерьера — Стадия: РП; Лист: 79; Листов: 79
Пров.						
ГИП						
						Смета ориентировочная (окончание) — М 6/м
Н. контр.						Кырпан Александр Сергеевич
Утв.						

выпуск 09.10.2026 № 147dabfd23 · стр. 91 из 110

11

Визуализации

Кырлан Александр Сергеевич

выпуск 09.10.2026 № 147dabfd23 · стр. 92 из 110

выпуск 09.10.2026 № 147dabfd23 · стр. 93 из 110



Планировочное решение · вид сверху

выпуск 09.10.2026 № 147dabfd23 · стр. 94 из 110



Гостиная



Гостиная · диван и кабинет

Квартира 65 м² · визуализация 3 из 18

выпуск 09.10.2026 № 147dabfd23 · стр. 95 из 110



Кухня-столовая

Квартира 65 м² · визуализация 4 из 18

выпуск 09.10.2026 № 147dabfd23 · стр. 96 из 110



Спальня

Квартира 65 м² · визуализация 5 из 18

выпуск 09.10.2026 № 147dabfd23 · стр. 98 из 110



Детская

Квартира 65 м² · визуализация 6 из 18



Прихожая

Квартира 65 м² · визуализация 7 из 18

выпуск 09.10.2026 № 147dabfd23 · стр. 99 из 110



Ванная комната

Квартира 65 м² · визуализация 8 из 18

выпуск 09.10.2026 № 147dabfd23 · стр. 100 из 110

выпуск 09.10.2026 № 147dabfd23 · стр. 101 из 110



room-bath-wB



room-bedroom-wD

Квартира 65 м² · визуализация 10 из 18



room-corridor-wA

Квартира 65 м² · визуализация 11 из 18

выпуск 09.10.2026 № 147dabfd23 · стр. 103 из 110

выпуск 09.10.2026 № 147dabfd23 · стр. 104 из 110



room-corridor-wC



room-hall-wB

Квартира 65 м² · визуализация 13 из 18



room-kids-wA

Квартира 65 м² · визуализация 14 из 18



room-kids-wC

Квартира 65 м² · визуализация 15 из 18

выпуск 09.10.2026 № 147dabfd23 · стр. 107 из 110



room-kids-wD

Квартира 65 м² · визуализация 16 из 18



room-living-wB

Квартира 65 м² · визуализация 17 из 18

выпуск 09.10.2026 № 147dabfd23 · стр. 109 из 110



room-wc-wC

Квартира 65 м² · визуализация 18 из 18

выпуск 09.10.2026 № 147dabfd23 · стр. 110 из 110