
LINEA

ДИЗАЙН-ПРОЕКТ ИНТЕРЬЕРА

Дом 147 м²

Средиземноморский

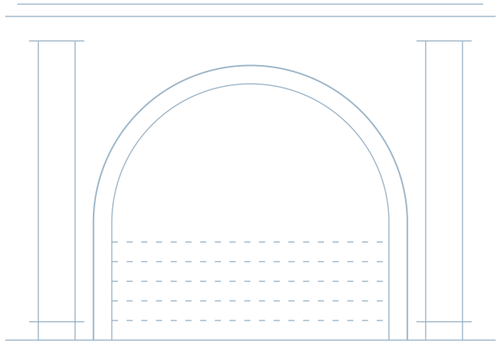


ПАЛИТРА ОТДЕЛКИ

G503	Little Greene	NCS S 0502-Y	NCS S 5020-G90	NCS S 3050-R80
53 %	33 %	5 %	2 %	2 %

АВТОР ПРОЕКТА

Кырлан Александр Сергеевич

Ноябрь 2026

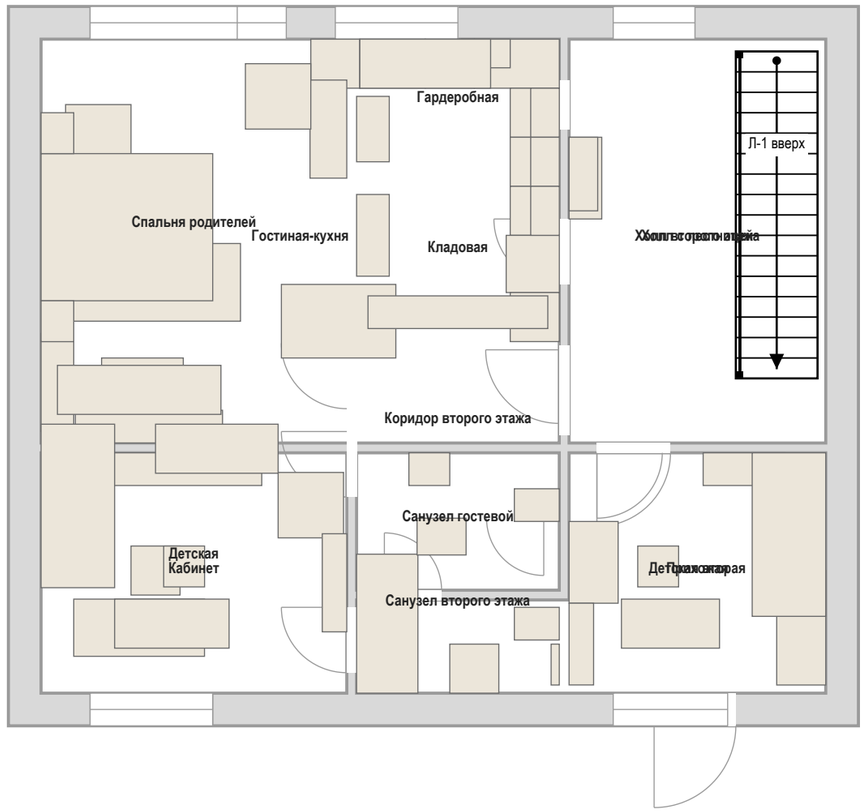

План расстановки мебели · М 1:75

ОБЩАЯ ПЛОЩАДЬ	ПОМЕЩЕНИЙ	СТАДИЯ	ШИФР	ОСНОВА
147,36 м²	13, из них жилых 5	Проект · предварительно	ГД-2026-012-АИ	план заказчика, без обмера

Как оставить правку: кнопка «Правка к этому листу» в правом верхнем углу любого листа · все листы проекта: дизайн-студия-квартир.рф/review.html?p=gost-dom120

выпуск 04.11.2026 № 406ed8a6ce · стр. 1 из 136

Объект

Дом 120 м²: 147,36 м², помещений 13, из них жилых 5.

Стиль: средиземноморский 60 %, скандинавский 40 %. Стадия: предварительный альбом без обмера, планировка по плану заказчика.

Открытых вопросов 9, конфликтов разделов 0; изменений утверждено 0, ждут подписи 2.

Розетки и выводы

48 розеток (рамок 43), 6 выводов кабеля под технику и свет, 17 групп щита — всё с высотами от чистого пола: листы 50, 51.

Что решено (подписано вами)

Подписанных решений пока нет.

Что ждёт вашего ответа

К-1 — Бриф задаёт 11 помещений с габаритами и этажами, но не их взаимное расположение, контур дома и толщины стен: раскладка этажей, контур 9600 × 8000 и перегородки подобраны…

К-2 — Высота потолка 2900 мм — по брифу (не замерена).

К-3 — Лестница по брифу — из холла 1-го этажа.

К-4 — Разрешённая мощность дома по ТУ неизвестна, принята 15 кВт.

К-5 — Тип дома, материал и конструкция стен и перекрытия, несущие стены, положение стояков, выпусков канализации и вентканалов в брифе не заданы.

К-6 — Источник отопления и горячей воды (котёл: газ / электро, его место, котельная) брифом не задан.

К-7 — Климатический подрайон (СП 131.13330) не задан: принят не северный — жилые комнаты и кухня под потолком от 2,5 м (СП 54, п. 5.12).

К-8 — Кухня (пом. 1): мойка М_02 и модули М_01, М_03 стоят под окном 1500 × 1500 стены А с низом проёма +0,900 — подоконник в уровне столешницы (+0,900).

К-9 — Умывальник С_05 (пом. 13 «Санузел второго этажа»), выпуск К1-4 Ø50: трасса до Ст К1-1 (2,54 м) идёт под дверным проёмом Д-8 — короб над полом там не поставить.

Предложено, ждёт подписи

ИЗ-1 — Ванна С_03 — вдоль стены Г (offset 500, x 3800…4550, y 6300…8000).

ИЗ-2 — М_19 и М_41 — у стены Г холлов (offset 1200).

выпуск 04.11.2026 № 406ed8a6ce · стр. 2 из 136

					Проект: Дом 120 м²
	Лист	№ док.	Подпись	Дата	Ваш проект на одной странице
Дизайнер	Кырлан А.С.			04.11.26	

Стадия	Лист	Листов
П	2	136

Список листов

Лист	Наименование
1	Титульный лист
2	Ваш проект на одной странице
3	Список листов
4	Список листов
5	Как читать альбом
6	План планировки от заказчика · 1-й этаж
7	План планировки от заказчика · 2-й этаж
8	План монтажный · 1-й этаж
9	План монтажный · 2-й этаж
10	Кухня (пом. 1). Монтажная схема
11	Кухня (пом. 1). Монтажная схема
12	Шкафы. Монтажная схема. Лист 1 из 2
13	Шкафы. Монтажная схема. Лист 2 из 2
14	Карта покрытий стен · 1-й этаж
15	Карта покрытий стен · 2-й этаж
16	Колерная карта · 1-й этаж
17	Колерная карта · 2-й этаж
18	Колерная карта
19	План размещения мебели и оборудования · 1-й этаж
20	План размещения мебели и оборудования · 2-й этаж
21	Спецификация мебели и оборудования
22	Спецификация мебели и оборудования (продолжение)
23	Спецификация мебели и оборудования (продолжение)
24	Спецификация мебели и оборудования (продолжение)
25	Ведомости изделий, техники и фурнитуры
26	План выводов сантехники · 1-й этаж
27	План выводов сантехники · 2-й этаж
28	Схема разводки водопровода и канализации · 1-й этаж
29	Схема разводки водопровода и канализации · 2-й этаж
30	Аксонометрическая схема В1 (холодное водоснабжение)
31	Аксонометрическая схема Т3 (горячее водоснабжение)
32	Аксонометрическая схема К1 (канализация)
33	Развёртки мокрых зон: выводы ВК. Гостиная-кухня
34	Развёртки мокрых зон: выводы ВК. Санузел гостевой
35	Развёртки мокрых зон: выводы ВК. Санузел второго этажа (лист 1 из 2)
36	Развёртки мокрых зон: выводы ВК. Санузел второго этажа (лист 2 из 2)
37	Спецификация сантехнического оборудования
38	Раскладка плитки. Санузел гостевой. Развёртки стен
39	Раскладка плитки. Санузел второго этажа. Развёртки стен
40	План размещения дверей · 1-й этаж
41	План размещения дверей · 2-й этаж
42	Лестница Л-1
43	План потолков · 1-й этаж
44	План потолков · 2-й этаж
45	Разрезы и узлы потолков
46	Разрезы и узлы потолков (продолжение)
47	Разрезы и узлы потолков (продолжение)
48	Сечения потолков М 1:10
49	Сечения потолков М 1:10
50	Однолинейная схема щита
51	Однолинейная схема щита (продолжение)
52	План розеток и электровыводов · 1-й этаж
53	План розеток и электровыводов · 2-й этаж
54	План слаботочных сетей · 1-й этаж
55	План слаботочных сетей · 2-й этаж
56	План освещения · 1-й этаж
57	План освещения · 2-й этаж
58	Техническое задание на подбор светильников
59	Управление светильниками · 1-й этаж
60	Управление светильниками · 2-й этаж
61	План вентиляции · 1-й этаж
62	План вентиляции · 2-й этаж
63	План отопления · 1-й этаж
64	План отопления · 2-й этаж
65	План покрытий пола · 1-й этаж
66	План покрытий пола · 2-й этаж
67	Раскладка плитки. Планы полов
68	Раскладка плитки. Прихожая. Фартук кухни

					Проект: Дом 120 м²
	Лист	№ док.	Подпись	Дата	Список листов
Дизайнер	Кырлан А.С.			04.11.26	Стадия: П; Лист: 3; Листов: 136

выпуск 04.11.2026 № 406ed8a6ce · стр. 3 из 136

Список листов (продолжение)

Лист	Наименование
69	Развёртка стены А. Гостиная-кухня (пом. 1), кухонный фронт
70	Привязки электроточек и выводов ВК, стена А. Гостиная-кухня (пом. 1)
71	Развёртка стены Б. Гостиная-кухня (пом. 1), кухонный фронт
72	Привязки электроточек, стена Б. Гостиная-кухня (пом. 1)
73	Развёртка стены В. Гостиная-кухня (пом. 1)
74	Привязки электроточек, стена В. Гостиная-кухня (пом. 1)
75	Развёртка стены Г. Гостиная-кухня (пом. 1)
76	Развёртка стены А. Холл с лестницей (пом. 2)
77	Развёртка стены В. Холл с лестницей (пом. 2)
78	Развёртка стены Г. Холл с лестницей (пом. 2)
79	Развёртка стены А. Кабинет (пом. 3)
80	Развёртка стены Б. Кабинет (пом. 3)
81	Развёртка стены В. Кабинет (пом. 3)
82	Развёртка стены Г. Кабинет (пом. 3)
83	Развёртки стен А, Б. Санузел гостевой (пом. 4)
84	Привязки электроточек и выводов ВК, стена А. Санузел гостевой (пом. 4)
85	Развёртки стен В, Г. Санузел гостевой (пом. 4)
86	Развёртка стены А1. Прихожая (пом. 5)
87	Развёртка стены А2. Прихожая (пом. 5)
88	Развёртка стены Б. Прихожая (пом. 5)
89	Развёртка стены В. Прихожая (пом. 5)
90	Развёртки стен Г1, Г2. Прихожая (пом. 5)
91	Развёртка стены А. Спальня родителей (пом. 6)
92	Развёртка стены Б. Спальня родителей (пом. 6)
93	Развёртка стены В. Спальня родителей (пом. 6)
94	Развёртка стены Г. Спальня родителей (пом. 6)
95	Привязки электроточек, стена Г. Спальня родителей (пом. 6)
96	Развёртка стены А. Детская (пом. 7)
97	Развёртка стены Б. Детская (пом. 7)
98	Развёртка стены В. Детская (пом. 7)
99	Развёртка стены Г. Детская (пом. 7)
100	Развёртки стен А, Б. Гардеробная (пом. 8)
101	Развёртки стен В, Г. Гардеробная (пом. 8)
102	Развёртки стен Б, В. Кладовая (пом. 9)
103	Развёртка стены Г. Кладовая (пом. 9)
104	Развёртка стены А. Холл второго этажа (пом. 10)
105	Развёртка стены В. Холл второго этажа (пом. 10)
106	Развёртка стены Г. Холл второго этажа (пом. 10)
107	Развёртки стен А, В. Коридор второго этажа (пом. 11)
108	Развёртка стены Г. Коридор второго этажа (пом. 11)

Лист	Наименование
109	Развёртка стены А. Детская вторая (пом. 12)
110	Развёртка стены Б. Детская вторая (пом. 12)
111	Развёртка стены В. Детская вторая (пом. 12)
112	Развёртка стены Г. Детская вторая (пом. 12)
113	Развёртки стен А, Б. Санузел второго этажа (пом. 13)
114	Привязки электроточек и выводов ВК, стены А, Б. Санузел второго этажа (пом. 13)
115	Развёртки стен В, Г. Санузел второго этажа (пом. 13)
116	Открытые вопросы, принятые допущения и конфликты. Лист 1 из 2
117	Открытые вопросы, принятые допущения и конфликты. Лист 2 из 2
Д_1	Шкаф-купе М_24
Д_2	Шкаф распашной М_29
Д_3	Шкаф распашной М_34
Д_4	Система хранения М_37
Д_5	Система хранения М_38
Д_6	Система хранения М_39
Д_7	Система хранения М_40
Д_8	Шкаф распашной М_44
Д_9	Система хранения М_46
Д_10	Кухня (пом. 1). Развёртка гарнитура
Д_11	Кухня (пом. 1). Развёртка гарнитура
С1	Ведомость отделки помещений. Лист 1 из 3
С2	Ведомость отделки помещений. Лист 2 из 3
С3	Ведомость отделки помещений. Лист 3 из 3
С4	Спецификация отделочных материалов
С5	Спецификация отделочных материалов
С6	Список покупок
С7	Список покупок (окончание)
С8	Узлы

Общие указания

1. Размеры даны в мм от чистовых поверхностей стен: слой штукатурки 20 мм по блоку и 5 мм шпаклёвки по ГКЛ учтён. Перед заказом встроенной мебели — контрольный обмер после штукатурки.
2. Привязки мебели — от стен и углов помещения, а не от другой мебели.
3. Розетки, выводы и выключатели под мебель — см. лист 52 «План розеток и электровыводов · 1-й этаж»; сантехприборы и выводы воды — лист 26.
4. План расстановки не является документацией для изготовления мебели: изделия — по чертежам мебельщика; покупную мебель заменять только на изделия не больше габарита из спецификации (лист 21).
5. Встроенная мебель «стена в стену» — с зазором 10 мм с каждой стороны или с компенсаторами.
6. Развёртки — вид на стену изнутри помещения, по часовой стрелке; расположение стен на схеме листа развёртки; размеры — в мм по чистовым поверхностям; отметки — в м от ±0,000 (чистый пол 1-го этажа); высоты Н — от чистого пола помещения до оси изделия, у декора — до центра.
7. Красная цепочка — привязки электроточек и выводов по осям от угла чистовых стен; высота Н — у знака, от чистого пола до оси; высоты мебели, проёмов и границ отделки колонкой отметок слева. Стена с 5 и более точками или с мелкими звеньями привязок показана двумя видами: архитектурная развёртка (мебель, отделка, проёмы, высоты) и вид «Привязки» на отдельном листе — точки и выводы с марками, одна цепочка по осям и таблица привязок (каждая точка — строка).
8. У знака электроточки: марка (Р — розетка, S — выключатель, Св — светильник, ЭВ вывод кабеля), ×N — число постов в рамке, гр. — группа щита, Н — высота оси от чистого пола, мм; группы по клавишам выключателя — на листе выключателей.
9. Схема мебели, приборов и декора не является технической документацией для производства мебели; габариты — по паспортам изделий.
10. Марки позиций: М_NN — мебель, ОБ_NN — оборудование, С_NN — сантехника; О-N отделка (ведомость отделочных материалов, серия С).
11. Размеры мебели и изделий на заказ уточнить по месту после отделочных работ.

					Проект: Дом 120 м²
	Лист	№ док.	Подпись	Дата	Список листов
Дизайнер	Кырлан А.С.			04.11.26	Стадия: П · Лист: 4 · Листов: 136

Что в альбоме

Альбом — дизайн-проект с рабочими чертежами для ремонта. Листы идут в порядке работ: титул и вводные, реестр открытых вопросов и решений, планы (обмер, монтаж стен, мебель, двери, потолки, полы), инженерия (сантехника, электрика, вентиляция и отопление), развёртки стен с визуализациями помещений, чертежи мебели, ведомости материалов и узлы.

Вам как заказчику — титул, эта вводная, «Ваш проект на одной странице», реестр вопросов, план мебели, визуализации и развёртки, ведомости мебели и материалов. Подрядчику — всё остальное: монтажные планы, привязки выводов и розеток, узлы, ведомости объёмов.

Знаки на листах

Без знака — решение утверждено или подтверждено обмером.

Что проверить до ремонта

1. Розетки у кровати и рабочего места: хватает ли их с каждой стороны кровати и над столом (план розеток — листы электрики).

2. Выводы под технику — варочная панель, духовка, посудомойка, стиральная машина, бойлер: совпадают ли с выбранными моделями (листы 21, 22, 23, 24).

3. Высоты розеток, выключателей и выводов даны от чистого пола: если мебель или техника будут другими — скажите до штробления стен.

Номера записей

К-N — открытый вопрос: чего не хватает или что выбрать (варианты и рекомендация — в тексте). Пока ответа нет, действует строка «если решения нет».

Кф-N — конфликт между разделами (например, мебель и радиатор в одном месте); закрывается решением, которое записывается как ИЗ-N.

ИЗ-N — изменение проекта: что было, что стало и кто утвердил. Изменение без подписи предложение.

Все записи — на листе реестра сразу после вводных; на других листах на них стоят ссылки.

Почему альбом предварительный

Обмера на объекте не было: размеры взяты с плана заказчика. Технические условия (мощность, вода, вентиляция дома) не получены, часть решений ждёт вашего ответа. Пока в реестре есть открытые вопросы, альбом предварительный — пометка в штампе снимается закрытием вопросов, а не стиранием.

Правку к любому листу можно оставить по кнопке «Правка к листу» или на сайте студии: дизайн-студия-квартир.рф — укажите номер листа и что изменить.


3 круга правок входят в цену; условия — в договоре и на странице вашего заказа на сайте студии.

Шифр проекта ГД-2026-012-АИ

					Проект: Дом 120 м²
	Лист	№ док.	Подпись	Дата	Как читать альбом
Дизайнер	Кырлан А.С.			04.11.26	

Стадия	Лист	Листов
П	5	136

выпуск 04.11.2026 № 406ed8a6ce · стр. 5 из 136

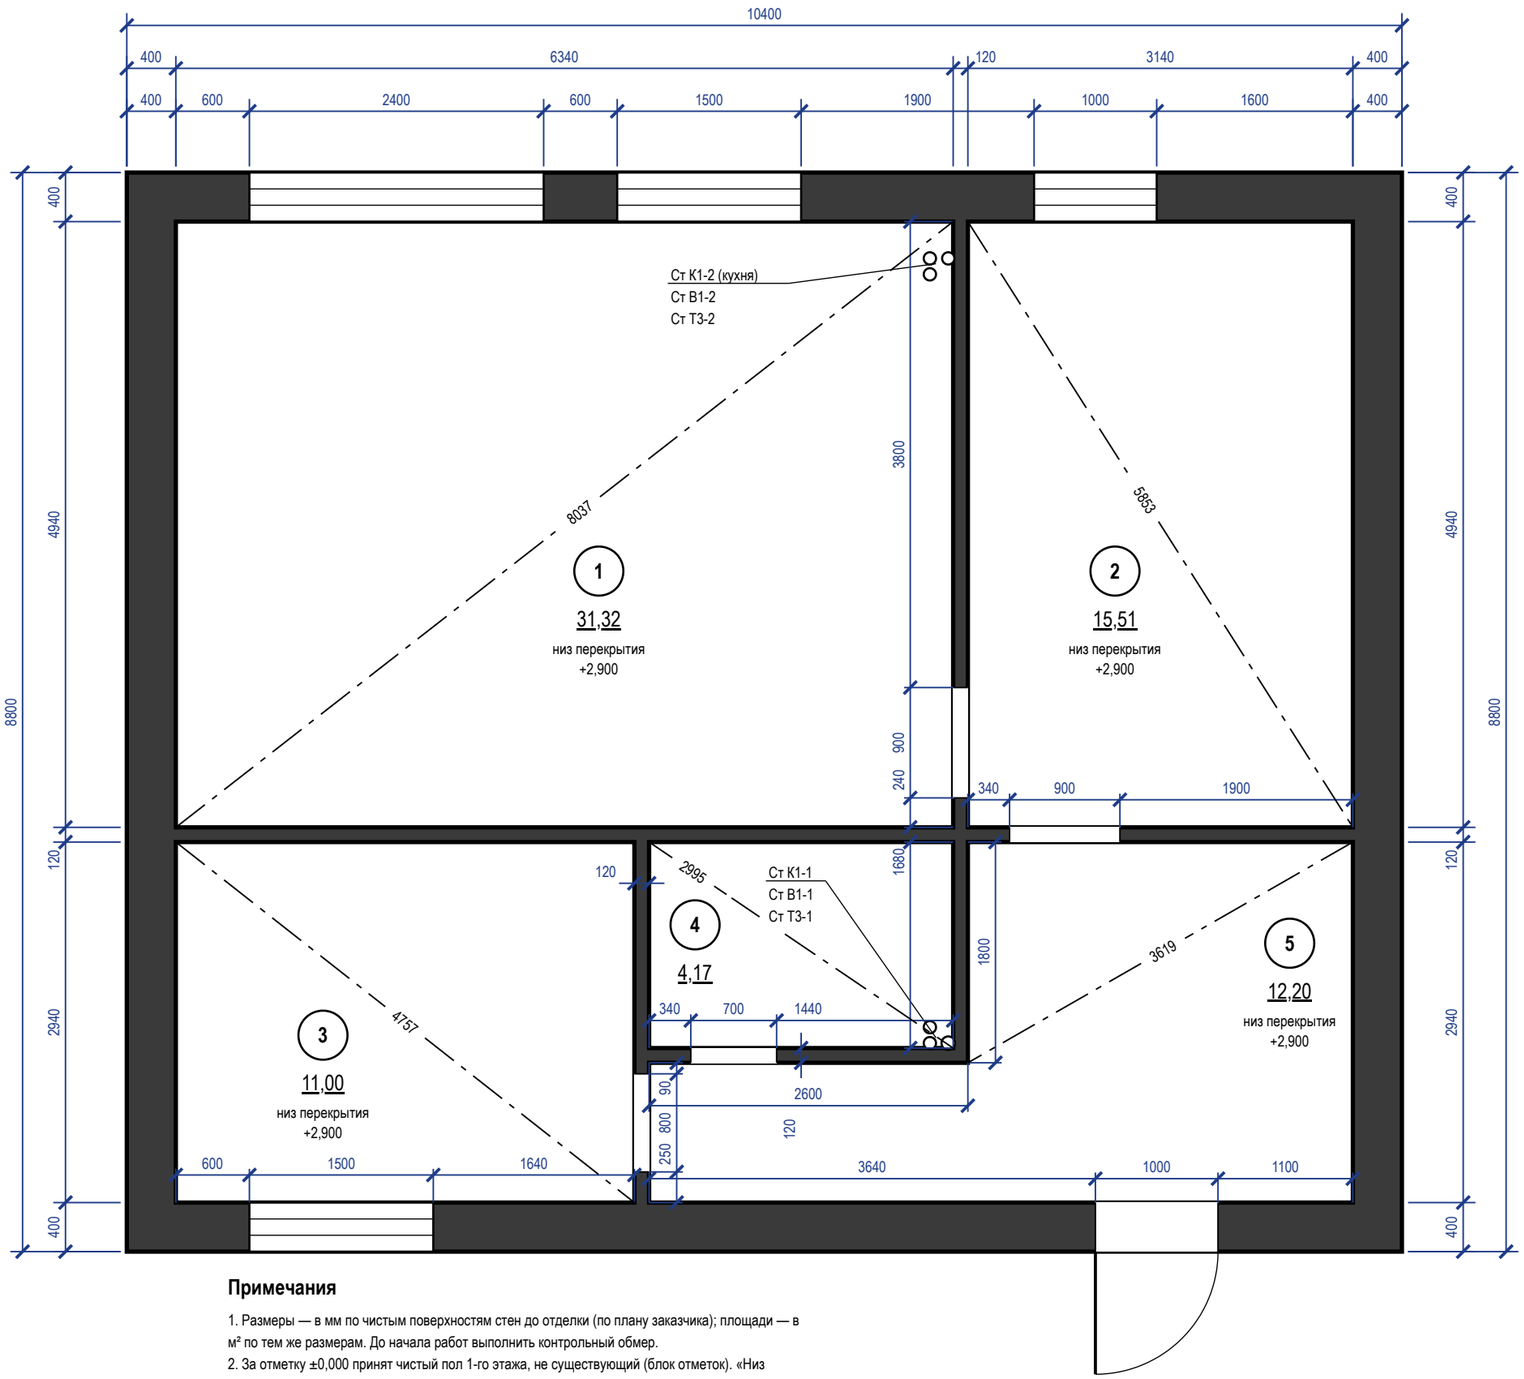

Экспликация помещений

№	Наименование	Площадь, м²
1	Гостиная-кухня	31,32
2	Холл с лестницей	15,51
3	Кабинет	11,00
4	Санузел гостевой	4,17
5	Прихожая	12,20
	Итого по этажу	**74,20**
	Итого по дому	**147,36**

Условные обозначения

- существующие стены (сечение)
- окно (рама, остекление)
- проём существующий, без заполнения (откосы)
- стояк: К1 — канализация, В1 — ХВС, Т3 — ГВС
- диагональ помещения — контроль прямоугольности
- (1) номер помещения, площадь м²

Отметки по высоте


±0,000	чистый пол пом. 1–3, 5; отсчёт высот
−0,015	чистый пол пом. 4, ниже на 15 мм
−0,064	верх плиты — расчёт, не замер (задание на обмер)
сущ. пол	снимается до плиты; не замерен (задание на обмер)

Примечания

1. Размеры — в мм по чистым поверхностям стен до отделки (по плану заказчика); площади — в м² по тем же размерам. До начала работ выполнить контрольный обмер.
2. За отметку ±0,000 принят чистый пол 1-го этажа, не существующий (блок отметок). «Низ перекрытия» у марки помещения — отметка низа перекрытия от ±0,000, как на развёртках и плане потолков (не высота потолка: потолок — по плану потолков).
3. Толщины стен: наружные 400 мм, перегородки 120 мм; отличающиеся толщины и уступы размерами на плане.
4. Несущие стены не определены: до технического заключения все стены считать несущими; проёмы и штробы в них не выполнять.
5. Дверные проёмы показаны без заполнения; высота дверных проёмов 2100 мм; низ окон (подоконник) 500, 900 мм от чистого пола, высота окон 1900, 1500 мм.
6. Диагонали — контрольные размеры; расхождение более 5 мм подписать на плане как перекос.
7. Размеры проверить на месте до начала работ; расхождение контрольных промеров ≤ 2 %.

					Проект: Дом 120 м²	**М 1:50**
	Лист	№ док.	Подпись	Дата	План планировки от заказчика · 1-й этаж	Стадия / Лист / Листов
Дизайнер	Кырлан А.С.			04.11.26		П / 6 / 136

выпуск 04.11.2026 № 406ed8a6ce · стр. 6 из 136

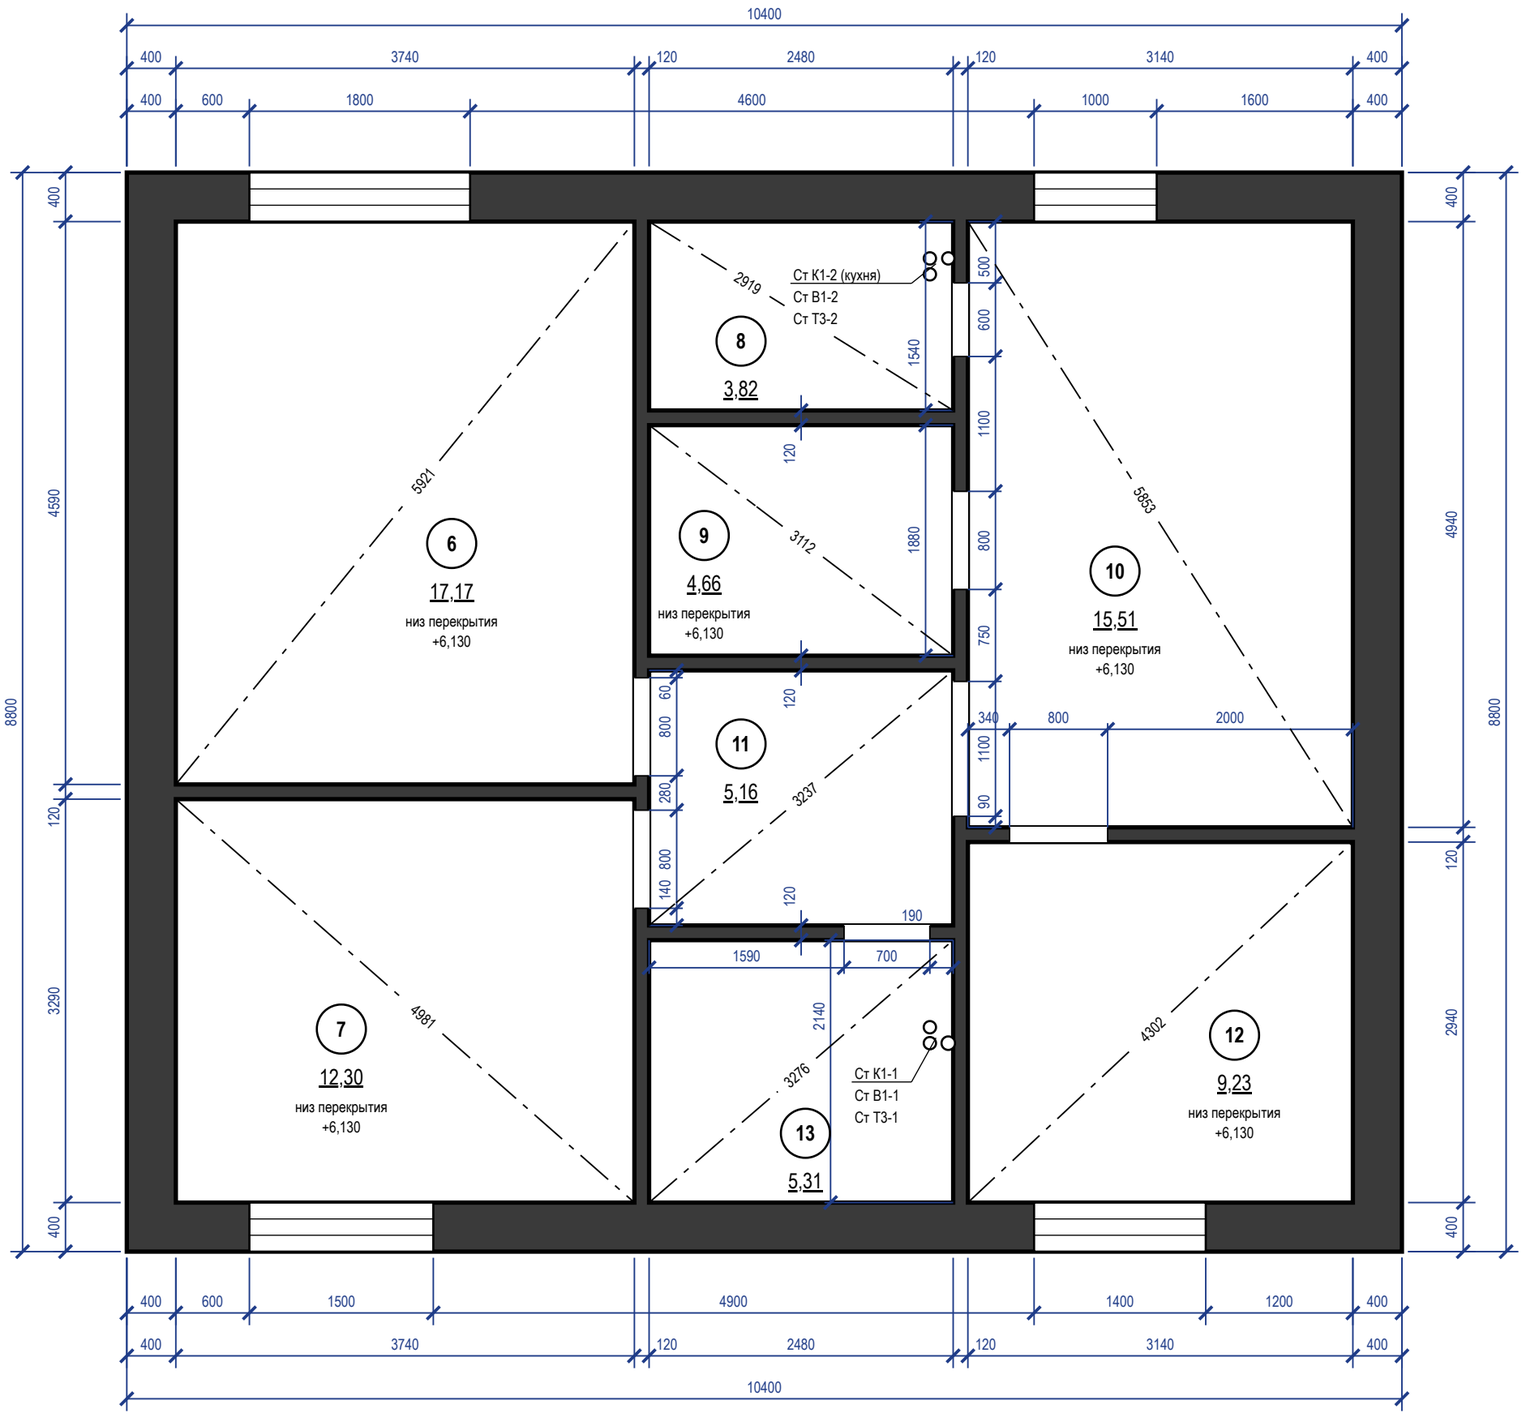

Экспликация помещений

№	Наименование	Площадь, м²
6	Спальня родителей	17,17
7	Детская	12,30
8	Гардеробная	3,82
9	Кладовая	4,66
10	Холл второго этажа	15,51
11	Коридор второго этажа	5,16
12	Детская вторая	9,23
13	Санузел второго этажа	5,31
	Итого по этажу	**73,16**

Условные обозначения

- существующие стены (сечение)
- окно (рама, остекление)
- проём существующий, без заполнения (откосы)
- стояк: К1 — канализация, В1 — ХВС, Т3 — ГВС
- диагональ помещения — контроль прямоугольности
- (1) номер помещения, площадь м²

Примечания

1. Размеры — в мм по чистым поверхностям стен до отделки (по плану заказчика); площади — в м² по тем же размерам. До начала работ выполнить контрольный обмер.
2. За отметку ±0,000 принят чистый пол 1-го этажа, не существующий; чистый пол этажа +3,230 (блок отметок). «Низ перекрытия» у марки помещения — отметка низа перекрытия от ±0,000, как на развёртках и плане потолков (не высота потолка: потолок — по плану потолков).
3. Толщины стен: наружные 400 мм, перегородки 120 мм; отличающиеся толщины и уступы — размерами на плане.
4. Несущие стены не определены: до технического заключения все стены считать несущими; проёмы и штробы в них не выполнять.
5. Дверные проёмы показаны без заполнения; высота дверных проёмов 2100 мм, проёмов без двери 2100 мм; низ окон (подоконник) 900 мм от чистого пола, высота окон 1500, 1450 мм.
6. Диагонали — контрольные размеры; расхождение более 5 мм подписать на плане как перекос.
7. Размеры проверить на месте до начала работ; расхождение контрольных промеров ≤ 2 %.

Отметки по высоте


±0,000	чистый пол 1-го этажа; отсчёт отметок
+3,230	чистый пол пом. 6–12 (2-й этаж)
+3,215	чистый пол пом. 13, ниже на 15 мм
+3,166	верх плиты — расчёт, не замер (задание на обмер)
сущ. пол	снимается до плиты; не замерен (задание на обмер)

	Лист	№ док.	Подпись	Дата
Дизайнер	Кырлан А.С.			04.11.26

Проект: Дом 120 м² — **М 1:50**

План планировки от заказчика · 2-й этаж

Стадия	Лист	Листов
П	7	136

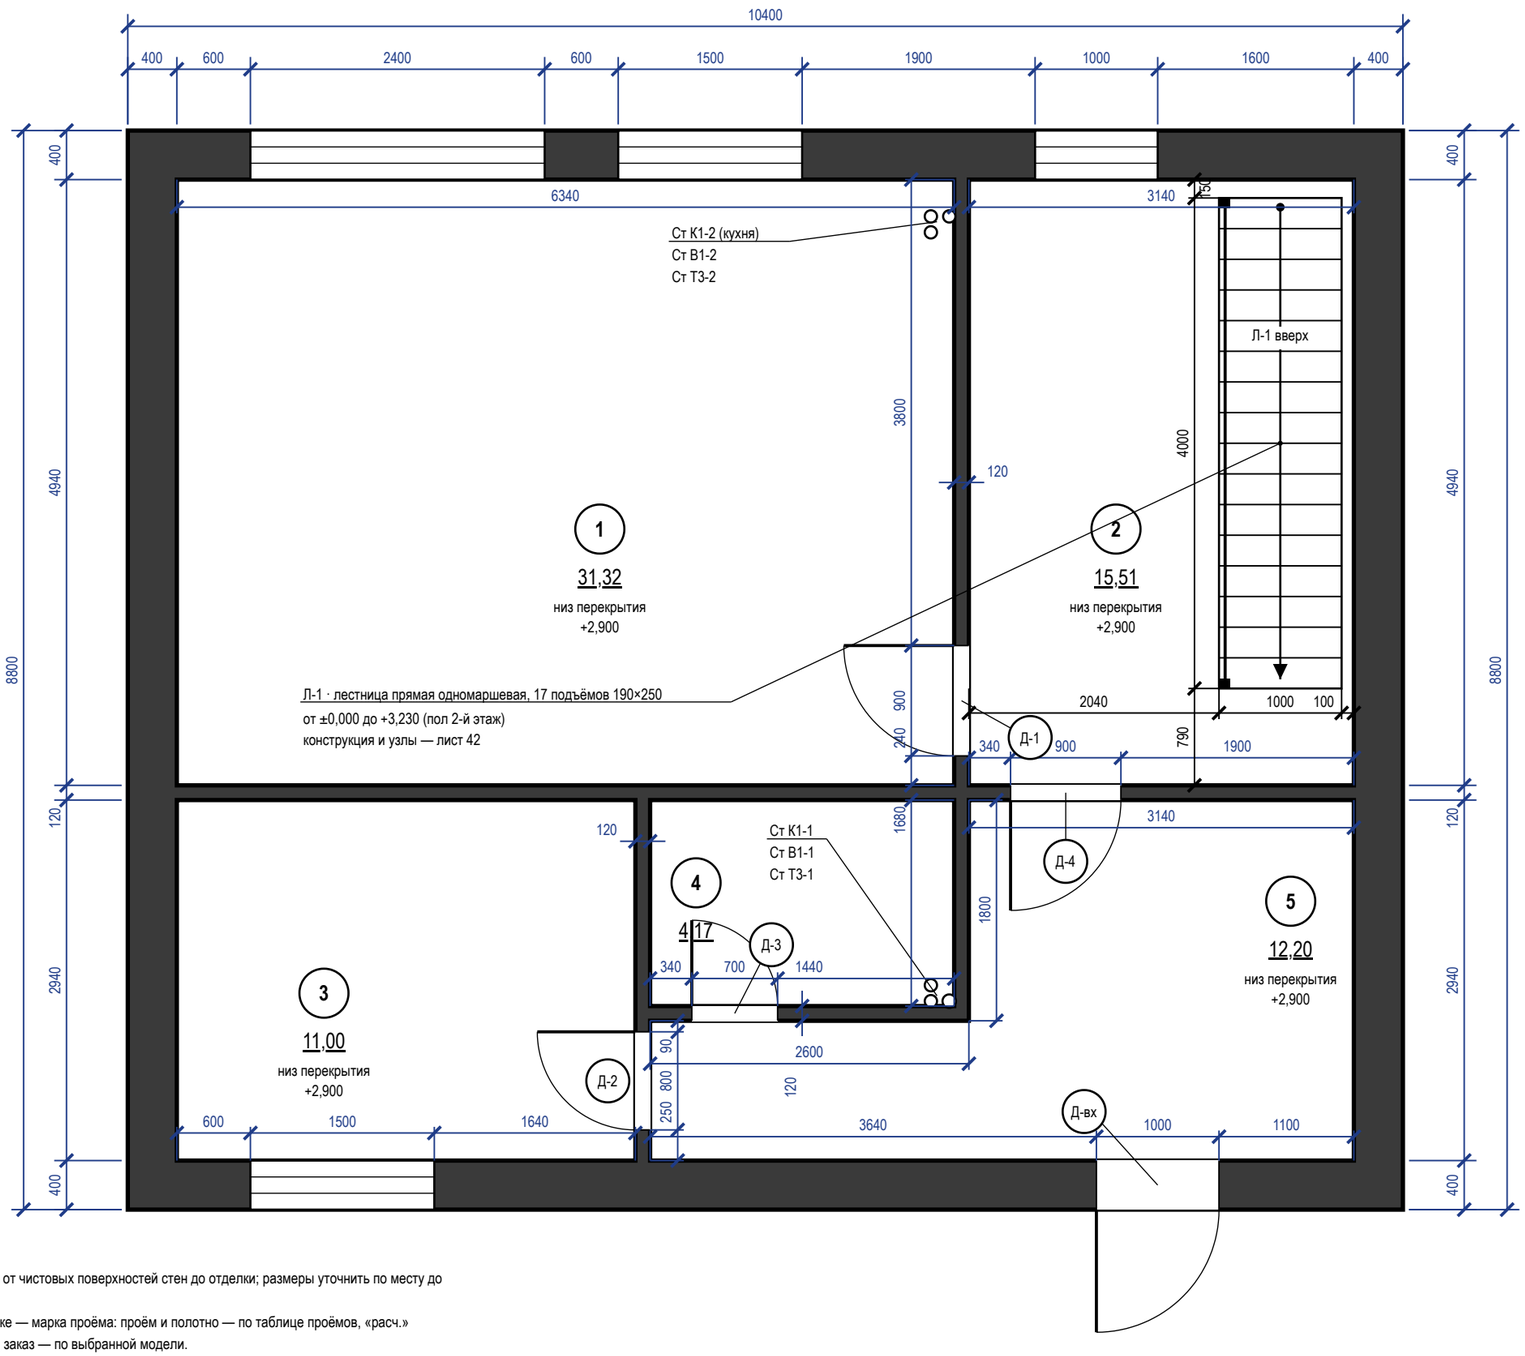

Экспликация помещений

№	Наименование	Площадь, м²
1	Гостиная-кухня	31,32
2	Холл с лестницей	15,51
3	Кабинет	11,00
4	Санузел гостевой	4,17
5	Прихожая	12,20
	Итого по этажу	**74,20**
	Итого по дому	**147,36**

Таблица проёмов

Марка	Наименование	Проём ш×в, мм	Полотно (расч.)
Д-вх	Дверь входная	1000×2100	блок — задать
Д-1	Дверь скрытого монтажа	900×2100	800×2000
Д-2	Дверь скрытого монтажа	800×2100	700×2000
Д-3	Дверь скрытого монтажа	700×2100	600×2000
Д-4	Дверь скрытого монтажа	900×2100	800×2000

Примечания


1. Размеры — в мм от чистовых поверхностей стен до отделки; размеры уточнить по месту до начала работ.
2. Д-N, ПР-N в кружке — марка проёма: проём и полотно — по таблице проёмов, «расч.» полотно по проёму, заказ — по выбранной модели.
3. Несущие стены не изменять: проёмы, ниши и штробы в них — только по техническому заключению.
4. «расч.» — полотно, выведенное из проёма по запасу каталогов; заказ — по таблице проёмов выбранной модели; Д-1, Д-2, Д-3, Д-4: проём 2100, а под полотно 2000 по каталогам нужен 2050–2080, под 2100 — 2150–2180: высоту проёма — по модели; Д-вх: входной блок по ГОСТ 31173-2016 — задать при выборе блока.

	Лист	№ док.	Подпись	Дата
Дизайнер	Кырлан А.С.			04.11.26

Проект: Дом 120 м² — **М 1:50**

План монтажный · 1-й этаж

Стадия	Лист	Листов
П	8	136

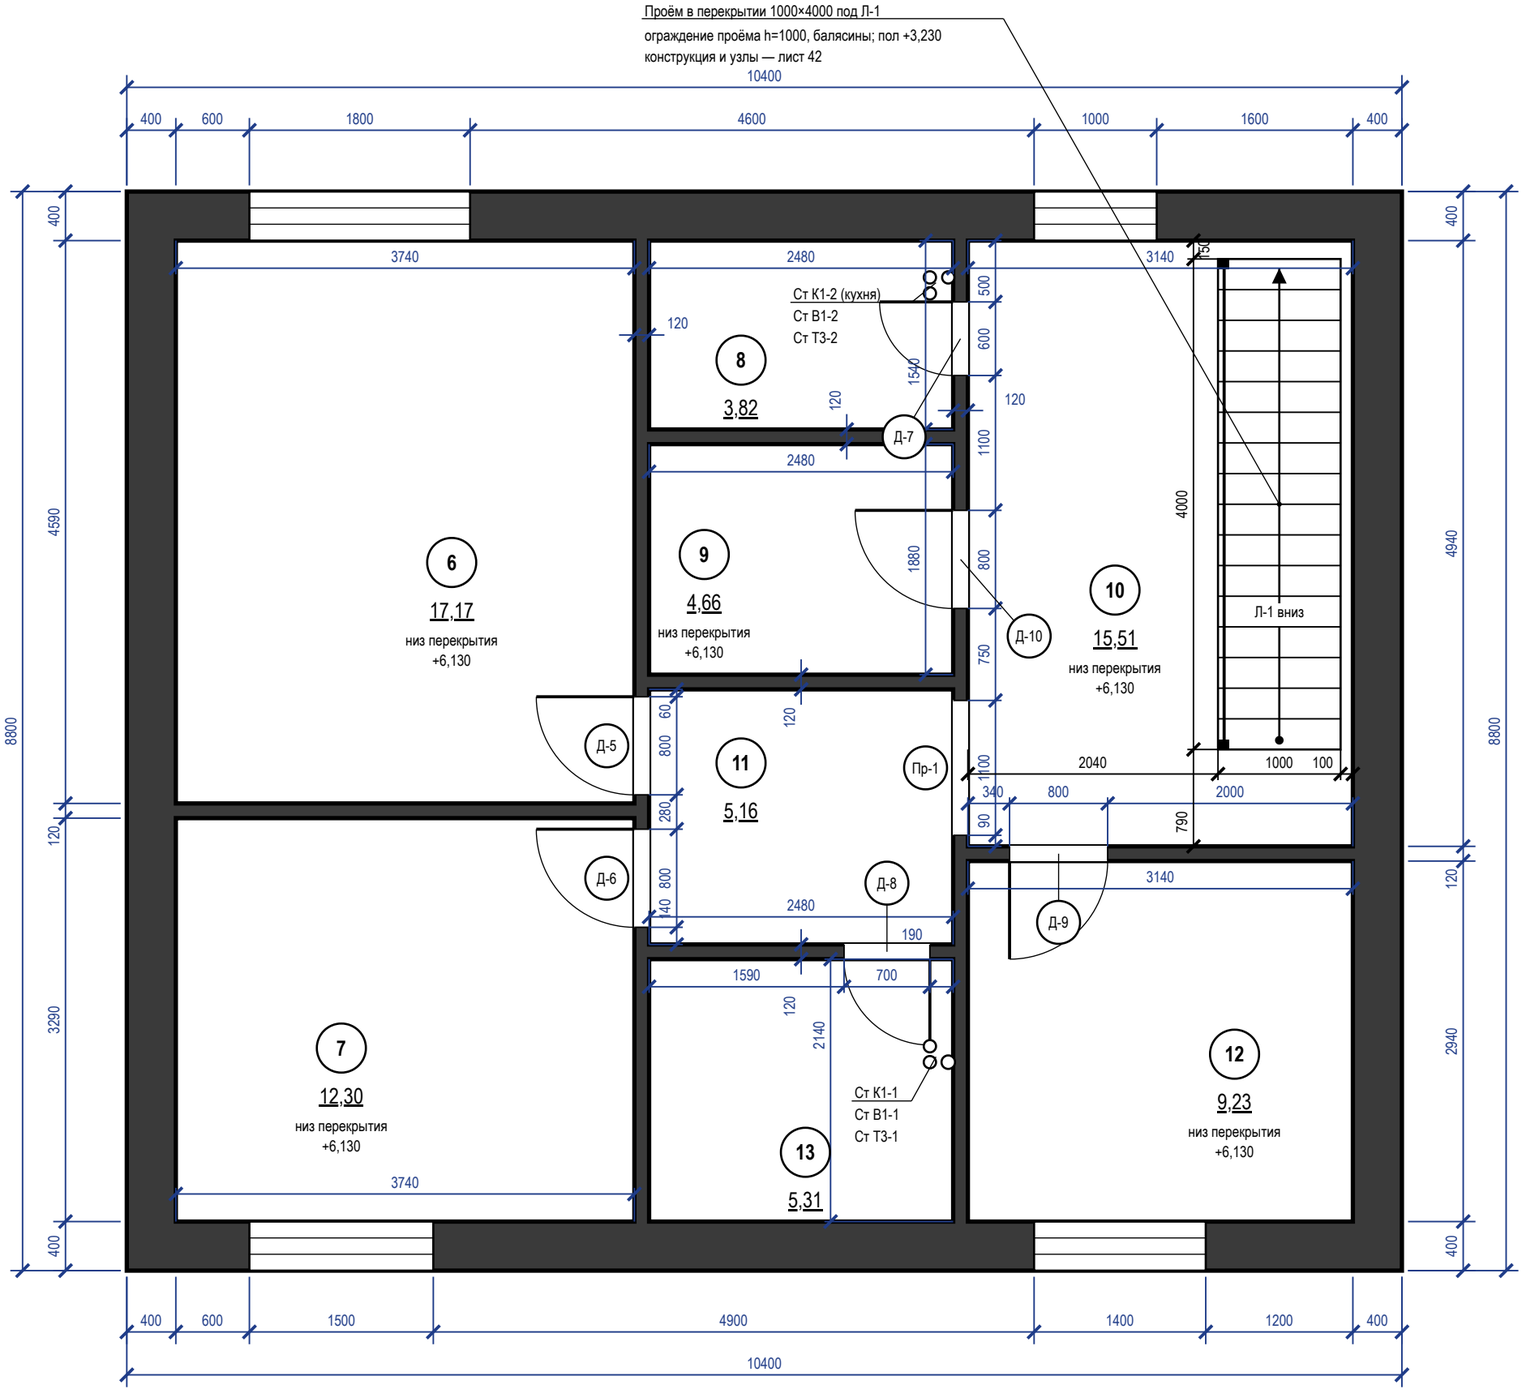

Экспликация помещений

№	Наименование	Площадь, м²
6	Спальня родителей	17,17
7	Детская	12,30
8	Гардеробная	3,82
9	Кладовая	4,66
10	Холл второго этажа	15,51
11	Коридор второго этажа	5,16
12	Детская вторая	9,23
13	Санузел второго этажа	5,31
	Итого по этажу	**73,16**

Таблица проёмов

Марка	Наименование	Проём ш×в, мм	Полотно (расч.)
Д-5	Дверь скрытого монтажа	800×2100	700×2000
Д-6	Дверь скрытого монтажа	800×2100	700×2000
Д-7	Дверь скрытого монтажа	600×2100	не задано (записи реестра нет)
Д-8	Дверь скрытого монтажа	700×2100	600×2000
Д-9	Дверь скрытого монтажа	800×2100	700×2000
Д-10	Дверь скрытого монтажа	800×2100	700×2000
Пр-1	Проём без заполнения	1100×2100	

Примечания

1. Размеры — в мм от чистовых поверхностей стен до отделки; размеры уточнить по месту до начала работ.
2. Д-N, ПР-N в кружке — марка проёма: проём и полотно — по таблице проёмов, «расч.» — полотно по проёму, заказ — по выбранной модели.
3. Несущие стены не изменять: проёмы, ниши и штробы в них — только по техническому заключению.
4. «расч.» — полотно, выведенное из проёма по запасу каталогов; заказ — по таблице проёмов выбранной модели; Д-5, Д-6, Д-8, Д-9, Д-10: проём 2100, а под полотно 2000 по каталогам нужен 2050–2080, под 2100 2150–2180: высоту проёма — по модели; Д-7: проём 600×2100 вне ряда полотен изделия — полотно задать при выборе модели.


	Лист	№ док.	Подпись	Дата
Дизайнер	Кырлан А.С.			04.11.26

Проект: Дом 120 м² — **М 1:50**


План монтажный · 2-й этаж

Стадия	Лист	Листов
П	9	136

Привязка выводов и крепление модулей

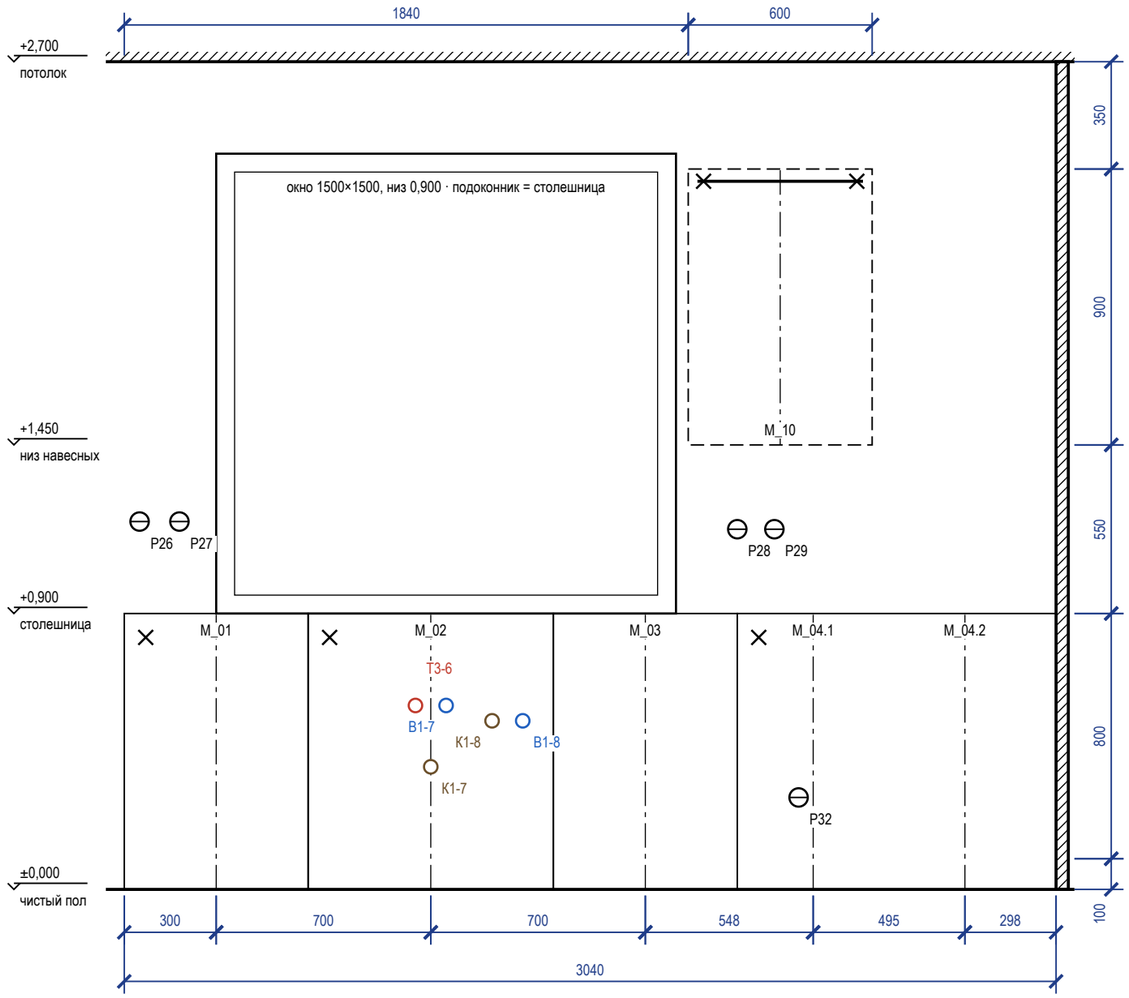

План столешницы

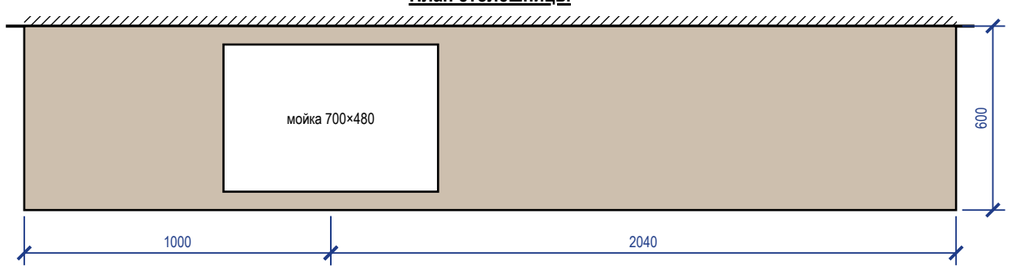

Привязка выводов к осям модулей

Код	Назначение	Модуль	От оси, мм	H, мм	Размещение
P26	розетка ×2 — фартук	M_01	−250	1200	над столешницей (фартук)
P27	розетка — фартук	M_01	−120	1200	над столешницей (фартук)
T3-6	T3 — межос. 100	M_02	−50	600	в модуле мойки
K1-7	K1 Ø50 — мойка	M_02	0	400	в модуле мойки
B1-7	B1 — межос. 100	M_02	+50	600	в модуле мойки
K1-8	K1 Ø40 — слив ПММ в шкафу мойки	M_02	+200	550	в модуле мойки
B1-8	B1 — кран ПММ в шкафу мойки	M_02	+300	550	в модуле мойки
P28	розетка ×2 — фартук	M_03	+300	1175	над столешницей (фартук)
P29	розетка — фартук	M_04.1	−126	1175	над столешницей (фартук)
P32	розетка — посудомоечная машина	M_04.1	−47	300	в соседнем модуле, за ящиком

Зазоры под отделку

Поверхность	Отделка	Зазор, мм	Учесть
фартук	керамогранит	10	от чернового основания до корпуса навесных и столешницы
стены	окраска	5	под штукатурку и шпаклёвку за пеналом
пол	инженерная доска		цоколь — после укладки пола, опоры ±20 мм

Условные обозначения


- нижний модуль, пенал (контур)
- невидимый контур: навесной модуль, корпус под столешницей
- ось модуля (от неё — привязка вывода)
- анкер / уголок крепления к стене
- розетка на стене
- вывод кабеля к технике
- B1 — вывод воды B1 / T3, канализации K1

Примечания


1. Окно над M_01, M_02, M_03: низ проёма на 900 мм от пола, столешница на 900 мм, под окном мойка M_02 — смеситель упирается в створку, открывающуюся внутрь; примыкание столешницы к откосу и подоконнику — до решения: нужно решение заказчика (створка глухая или поворотно-откидная, поднять подоконник); столешницу у окна не раскраивать до решения.
2. Выводы — по проекту электрики и ВК; привязка по горизонтали — от оси модуля (плюс — вправо по виду), по высоте — от чистого пола до оси вывода.
3. Пенал — уголки к стене 2 шт. сверху; нижние модули — стяжками между собой и уголком к стене; ряд выставить по уровню опорами цоколя.
4. Розетки над столешницей — не ниже 150 мм над ней и не за корпусом техники; розетка за ПММ, духовым шкафом и холодильником — только в соседнем модуле или в зоне цоколя с доступом.
5. Столешница — вырезы по шаблонам выбранных моделей мойки и варочной панели; торцы у стены — герметик, пристеночный плинтус.

					Проект: Дом 120 м² — **М 1:20**
	Лист	№ док.	Подпись	Дата	Кухня (пом. 1). Монтажная схема
Дизайнер	Кырлан А.С.			04.11.26	Стадия: П · Лист: 10 · Листов: 136

Привязка выводов и крепление модулей

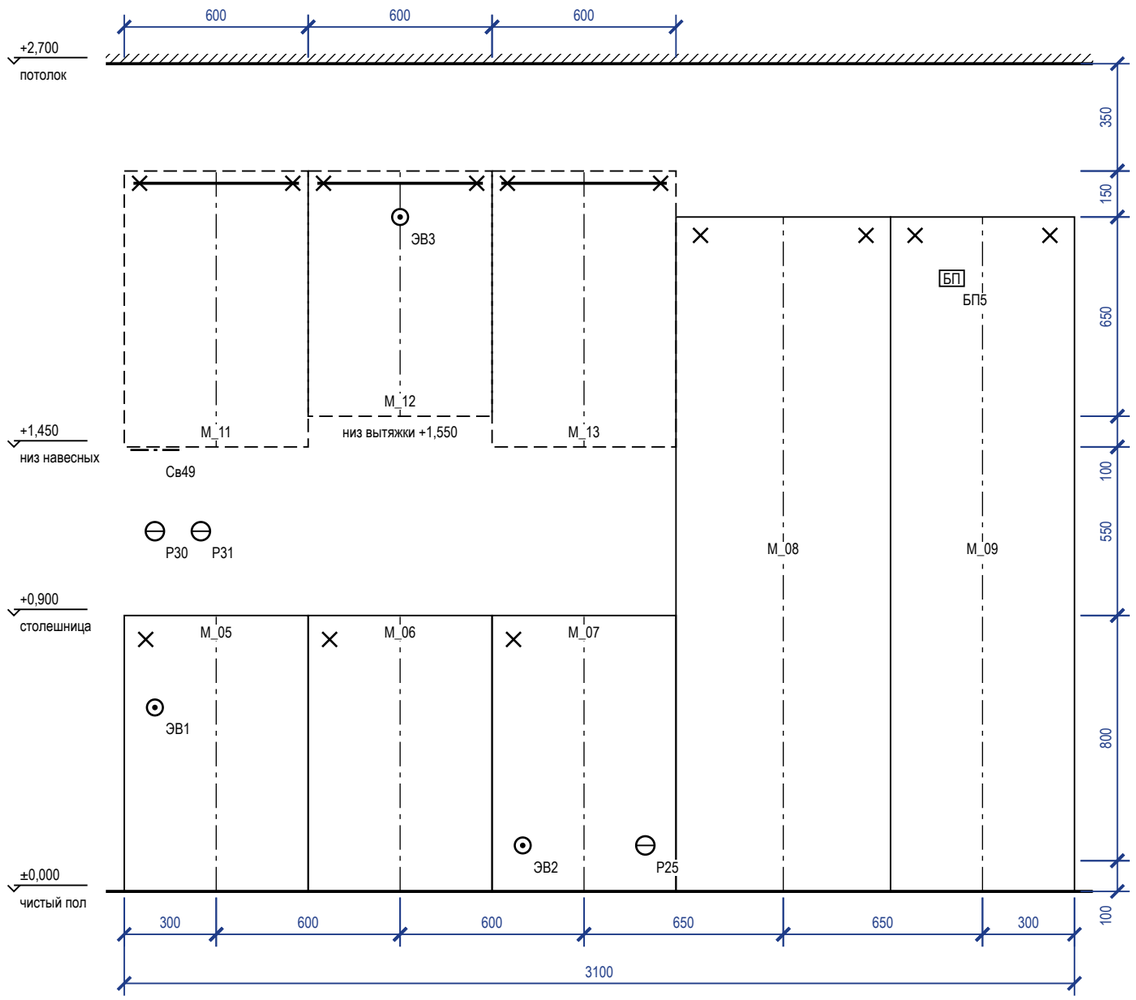

План столешницы

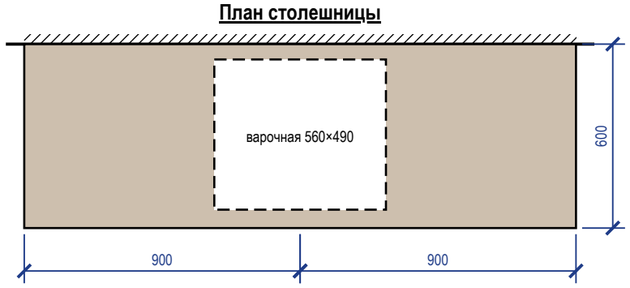

Привязка выводов к осям модулей

Код	Назначение	Модуль	От оси, мм	Н, мм	Размещение
Р30	розетка ×2 — фартук между мойкой и варочной	M_05	−200	1175	над столешницей (фартук)
ЭВ1	вывод кабеля — варочная панель M_06 (вывод в соседнем модуле M_05, за ящиком)	M_05	−200	600	в соседнем модуле, за ящиком
Св49	светодиодная лента — подсветка столешницы	M_05	−200	1440	в профиле по низу навесного модуля
Р31	розетка — фартук между мойкой и варочной	M_05	−50	1175	над столешницей (фартук)
ЭВ3	вывод кабеля — вытяжка	M_12	0	2200	в навесном модуле
ЭВ2	вывод кабеля — духовой шкаф	M_07	−200	150	в соседнем модуле, за ящиком
Р25	розетка — холодильник M_08 (розетка в соседнем модуле M_07, съёмная панель)	M_07	+200	150	в соседнем модуле, за ящиком
БП5	блок питания — в пенале M_09, верх, съёмная панель	M_09	−100	2000	за пеналом

Зазоры под отделку

Поверхность	Отделка	Зазор, мм	Учесть
фартук	керамогранит	10	от чернового основания до корпуса навесных и столешницы
стены	окраска	5	под штукатурку и шпаклёвку за пеналом
пол	инженерная доска		цоколь — после укладки пола, опоры ±20 мм

Условные обозначения

- нижний модуль, пенал (контур)
- невидимый контур: навесной модуль, корпус под столешницей
- ось модуля (от неё — привязка вывода)
- анкер / уголок крепления к стене
- розетка на стене
- вывод кабеля к технике
- B1 — вывод воды В1 / Т3, канализации К1


Примечания

1. Выводы — по проекту электрики и ВК; привязка по горизонтали — от оси модуля (плюс — вправо по виду), по высоте — от чистого пола до оси вывода.
2. Пенал — уголки к стене 2 шт. сверху; нижние модули — стяжками между собой и уголком к стене; ряд выставить по уровню опорами цоколя.
3. Розетки над столешницей — не ниже 150 мм над ней и не за корпусом техники; розетка за ПММ, духовым шкафом и холодильником — только в соседнем модуле или в зоне цоколя с доступом.
4. Столешница — вырезы по шаблонам выбранных моделей мойки и варочной панели; торцы у стены — герметик, пристеночный плинтус.


					Проект: Дом 120 м²	М 1:20
	Лист	№ док.	Подпись	Дата		
Дизайнер	Кырлан А.С.			04.11.26	Кухня (пом. 1). Монтажная схема	Стадия: П; Лист: 11; Листов: 136

выпуск 04.11.2026 № 406ed8a6ce · стр. 11 из 136


Шкаф-купе М_24 (пом. 5)

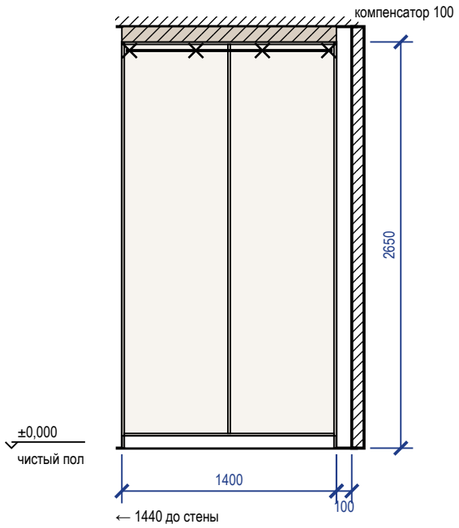


Шкаф распашной М_29 (пом. 6)

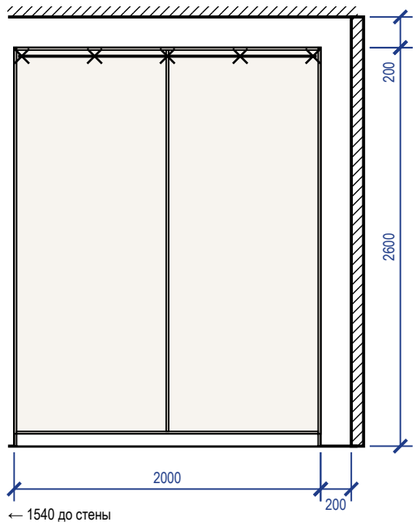


Шкаф распашной М_34 (пом. 7)

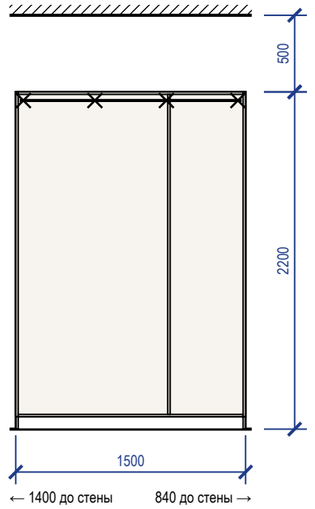

Система хранения М_37 (пом. 8)

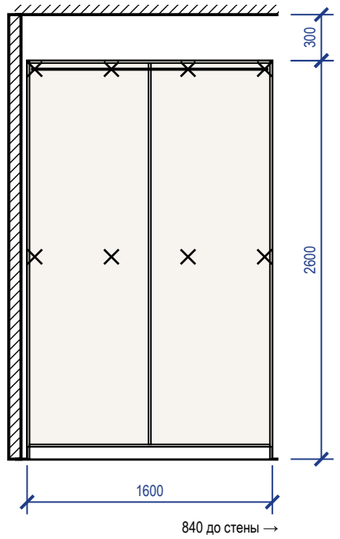

Система хранения М_38 пом. 8

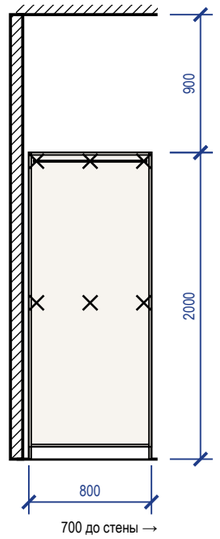

Крепление и зазоры под отделку (изделия листа 1)

Марка	Помещение, стена	Основание	Отделка стены	Зазор, мм	Крепёж по планке	От опрокидывания
М_24	Прихожая (5), стена Б	по основанию — см. таблицу крепежа	окраска	5	анкер 4 шт., шаг 433	уголки 2 шт.
М_29	Спальня родителей (6), стена В	по основанию — см. таблицу крепежа	окраска	5	анкер 5 шт., шаг 475	уголки 2 шт.
М_34	Детская (7), стена А	по основанию — см. таблицу крепежа	окраска	5	анкер 4 шт., шаг 467	уголки 2 шт.
М_37	Гардеробная (8), стена А	по основанию — см. таблицу крепежа	окраска	5	анкер 8 шт. (2 ряда)	уголки 2 шт.
М_38	Гардеробная (8), стена Г	по основанию — см. таблицу крепежа	окраска	5	анкер 6 шт. (2 ряда)	уголки 2 шт.

Крепёж по основанию стены

Основание стены	Крепёж
бетон, ж/б	анкер-шуруп 7,5×72 или дюбель 8×60 с шурупом 5×70
кирпич полнотелый	дюбель 8×80 с шурупом 5×90
газобетон, пазогребень	дюбель для газобетона 10×100 или химический анкер
гипсокартон	закладная до обшивки (брус 40×80 или фанера 18 мм), саморез в закладную

Условные обозначения


- анкер / уголок крепления к стене
- корпус и полки ЛДСП (вид на стену)
- компенсатор — короб до потолка

Примечания


1. Установочные размеры — от чистого пола и чистых стен; перед установкой контрольный замер после отделки.
2. Порядок: корпус выставить по уровню опорами цоколя → закрепить к стене по задней планке → навесить двери и фасады, отрегулировать зазоры → подогнать и закрепить компенсатор.
3. Анкеры — с шагом не более 500 мм, не ближе 50 мм от края планки; на ГКЛ только в закладную, установленную до обшивки.
4. Скрытые коммуникации под анкеры проверить детектором; трассы электрики по плану розеток.
5. Монтажная схема на 2 листах, лист 1 из 2; продолжение — на следующем листе схемы. Условные обозначения, таблица крепежа по основанию и примечания повторены на каждом листе.

					Проект: Дом 120 м²	М 1:40
	Лист	№ док.	Подпись	Дата		
Дизайнер	Кырлан А.С.			04.11.26	Шкафы. Монтажная схема. Лист 1 из 2	Стадия: П; Лист: 12; Листов: 136


Система хранения М_39 (пом. 9)

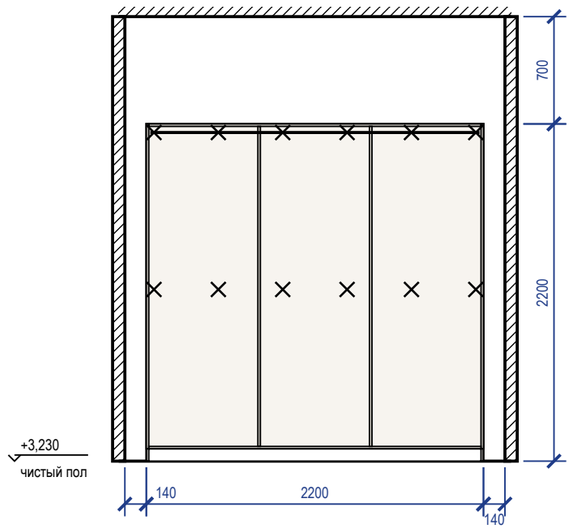


Система хранения М_40 пом. 9

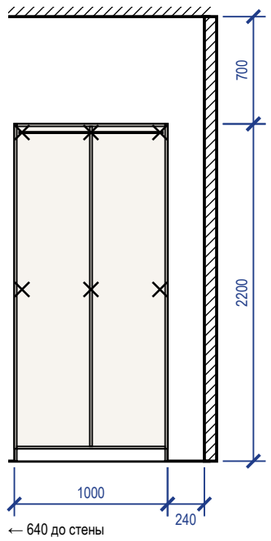

Шкаф распашной М_44 пом. 12

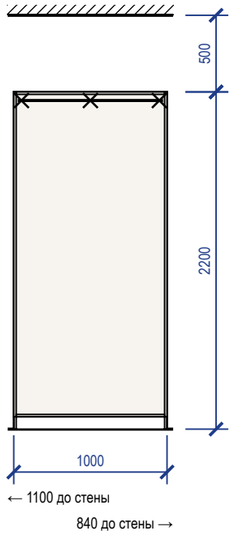

Система хранения М_46 пом. 12

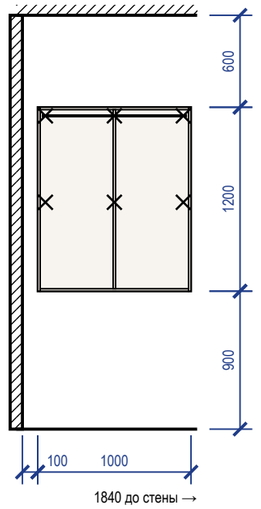

Крепление и зазоры под отделку (изделия листа 2)

Марка	Помещение, стена	Основание	Отделка стены	Зазор, мм	Крепёж по планке	От опрокидывания
М_39	Кладовая (9), стена В	по основанию — см. таблицу крепежа	окраска	5	анкер 12 шт. (2 ряда)	уголки 2 шт.
М_40	Кладовая (9), стена Г	по основанию — см. таблицу крепежа	окраска	5	анкер 6 шт. (2 ряда)	уголки 2 шт.
М_44	Детская вторая (12), стена Г	по основанию — см. таблицу крепежа	окраска	5	анкер 3 шт., шаг 450	уголки 2 шт.
М_46	Детская вторая (12), стена Г	по основанию — см. таблицу крепежа	окраска	5	анкер 6 шт. (2 ряда)	уголки 2 шт.

Крепёж по основанию стены

Основание стены	Крепёж
бетон, ж/б	анкер-шуруп 7,5×72 или дюбель 8×60 с шурупом 5×70
кирпич полнотелый	дюбель 8×80 с шурупом 5×90
газобетон, пазогребень	дюбель для газобетона 10×100 или химический анкер
гипсокартон	закладная до обшивки (брус 40×80 или фанера 18 мм), саморез в закладную

Условные обозначения


- анкер / уголок крепления к стене
- корпус и полки ЛДСП (вид на стену)
- компенсатор — короб до потолка

Примечания

1. Установочные размеры — от чистого пола и чистых стен; перед установкой контрольный замер после отделки.
2. Порядок: корпус выставить по уровню опорами цоколя → закрепить к стене по задней планке → навесить двери и фасады, отрегулировать зазоры → подогнать и закрепить компенсатор.
3. Анкеры — с шагом не более 500 мм, не ближе 50 мм от края планки; на ГКЛ только в закладную, установленную до обшивки.
4. Скрытые коммуникации под анкеры проверить детектором; трассы электрики по плану розеток.
5. Монтажная схема на 2 листах, лист 2 из 2. Условные обозначения, таблица крепежа по основанию и примечания повторены на каждом листе.

					Проект: Дом 120 м²	М 1:40
	Лист	№ док.	Подпись	Дата	Шкафы. Монтажная схема. Лист 2 из 2	Стадия / Лист / Листов
Дизайнер	Кырлан А.С.			04.11.26		П / 13 / 136

выпуск 04.11.2026 № 406ed8a6ce · стр. 13 из 136

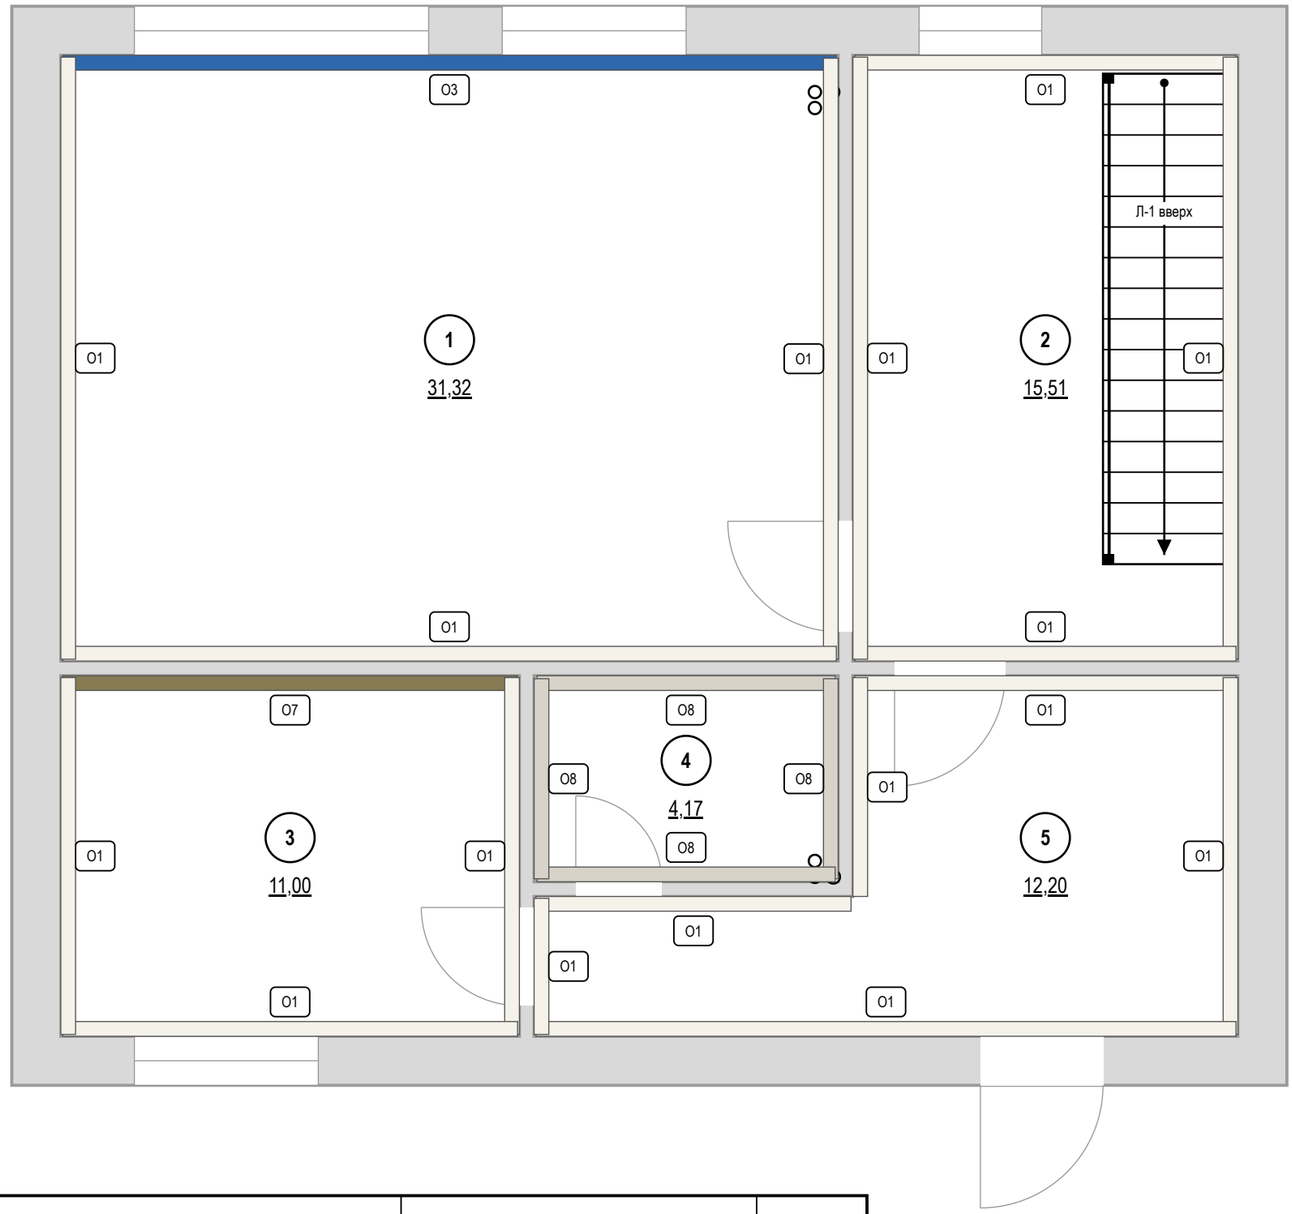


Покрытия стен

Марка	Покрытие	Помещение: S, м²	Итого, м²
О1	окраска Tikkurila · G503 «Calla»	1: 40,6; 2: 39,6; 3: 23,1; 5: 40,1	143,5
О3	окраска Tikkurila · S 3050-R80B «Эгейский синий»	1: 9,2	9,2
О7	окраска Tikkurila · S 5020-G90Y «Олива»	3: 10,4	10,4
О8	облицовка плиткой Atlas Concorde · A8UZ «Marvel Travertine» 600×1200 мм	4: 18,1	18,1

Площади — нетто, по развёрткам (за вычетом проёмов и фартука); высоты помещений — от чистого пола.

					Проект: Дом 120 м²	М 1:50
	Лист	№ док.	Подпись	Дата		
Дизайнер	Кырлан А.С.			04.11.26	Карта покрытий стен · 1-й этаж	Стадия: П; Лист: 14; Листов: 136

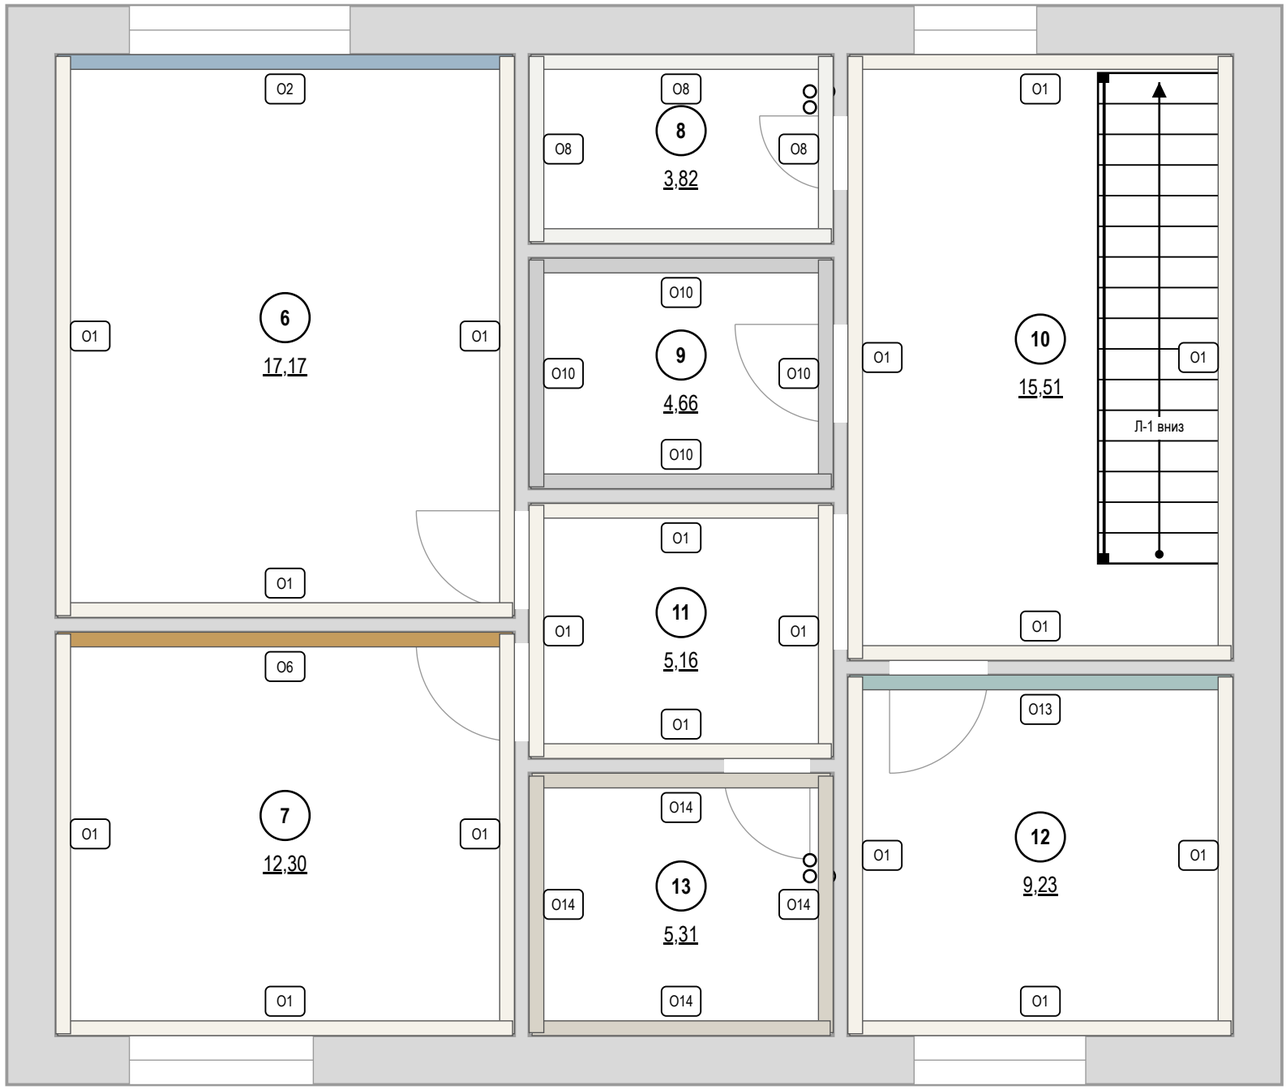

Покрытия стен

Марка	Покрытие	Помещение: S, м²	Итого, м²
O1	окраска Tikkurila · G503 «Calla»	6: 34,2; 7: 24,1; 10: 36,5; 11: 17,6; 12: 22,4	134,9
O2	окраска Farrow & Ball · No. 89 «Lulworth Blue — светлая морская лазурь»	6: 8,1	8,1
O6	окраска Farrow & Ball · No. 66 «India Yellow — охра / горчица итальянских фасадов»	7: 10,0	10,0
O8	окраска Little Greene · No. 222 «Loft White»	8: 21,7	21,7
O10	окраска Tikkurila · S 0502-Y	9: 23,3	23,3
O13	окраска Tikkurila · H440 «H440 Wave — бирюзово-голубая вода»	12: 6,7	6,7
O14	облицовка плиткой Atlas Concorde · A8UZ «Marvel Travertine» 600×1200 мм	13: 20,3	20,3

Площади — нетто, по развёрткам (за вычетом проёмов и фартука); высоты помещений — от чистого пола.

					Проект: Дом 120 м² — М 1:50
	Лист	№ док.	Подпись	Дата	
Дизайнер	Кырлан А.С.			04.11.26	Карта покрытий стен · 2-й этаж

Стадия	Лист	Листов
П	15	136

Колерная карта по помещениям

Помещение	Поверхность	Образец	Поз.	Система и код цвета	Производитель, линейка / материал, артикул	Блеск	Класс истирания	LRV	Площадь
1. Гостиная-кухня 31,32 м²	стены		**K1**	Tikkurila G503	Tikkurila	матовая	1	89	40,0 м²
	акцент А		**K2**	NCS S 3050-R80B	Tikkurila	матовая	1	≈13	10,3 м²
	потолок		**K3**	Little Greene No. 222	Little Greene · Absolute Matt	глубокомат.	2	92	31,3 м²
	пол		**KM1**	по образцу	Coswick · Вековые традиции · арт. 1167-4250				31,3 м²
	плинтус		**K4**	Tikkurila G503	МДФ · в цвет Tikkurila			89	21,7 м
	фартук		**KM2**	по образцу	керамогранит · аналог по хар.				1,9 м²
2. Холл с лестницей 15,51 м²	стены		**K1**	Tikkurila G503	Tikkurila	матовая	1	89	40,0 м²
	потолок		**K3**	Little Greene No. 222	Little Greene · Absolute Matt	глубокомат.	2	92	15,5 м²
	пол		**KM1**	по образцу	Coswick · Вековые традиции · арт. 1167-4250				15,5 м²
	плинтус		**K4**	Tikkurila G503	МДФ · в цвет Tikkurila			89	14,4 м
3. Кабинет 11 м²	стены		**K1**	Tikkurila G503	Tikkurila	матовая	1	89	23,0 м²
	акцент А		**K5**	NCS S 5020-G90Y	Tikkurila	матовая	1	≈20	10,5 м²
	потолок		**K3**	Little Greene No. 222	Little Greene · Absolute Matt	глубокомат.	2	92	11,0 м²
	пол		**KM1**	по образцу	Coswick · Вековые традиции · арт. 1167-4250				11,0 м²
	плинтус		**K4**	Tikkurila G503	МДФ · в цвет Tikkurila			89	12,6 м
4. Санузел гостевой 4,17 м²	стены		**KM3**	Marvel Travertine	Atlas Concorde · арт. A8UZ				18,5 м²
	потолок		**K6**	Little Greene No. 222	Little Greene · Intelligent Bathroom	матовая	1	92	4,2 м²
	пол		**KM4**	по образцу	керамогранит · аналог по хар.				4,2 м²
5. Прихожая 12,2 м²	стены		**K1**	Tikkurila G503	Tikkurila	матовая	1	89	40,6 м²
	потолок		**K3**	Little Greene No. 222	Little Greene · Absolute Matt	глубокомат.	2	92	12,2 м²
	пол		**KM5**	Marvel Travertine	Atlas Concorde · арт. A8UZ				12,2 м²
	плинтус		**K4**	Tikkurila G503	МДФ · в цвет Tikkurila			89	14,0 м

Перечень выкрасов на согласование

№	Код	Бренд / веер	Пом. / стена	Подложка	Формат	Статус
1	G503	Tikkurila	1, 2, 3, 5	ГКЛ с грунтом; МДФ под эмаль	600×1000; 300×600	к выполнению
2	S 3050-R80B	NCS Tikkurila	1 А	ГКЛ с грунтом	600×1000	к выполнению
3	No. 222	Little Greene	1, 2, 3, 4, 5	ГКЛ с грунтом	600×1000	к выполнению
4	S 5020-G90Y	NCS Tikkurila	3 А	ГКЛ с грунтом	600×1000	к выполнению

Примечания

1. Цвет на листе и на экране — ориентир. До покраски — выкрас на объекте: не меньше А3 (или лист ГКЛ), на грунте под эту краску, не на белой шпаклёвке, в 2 слоя; на обороте — код, бренд, веер, дата. Смотреть днём и вечером, рядом с образцами пола и плитки; к основному цвету стен — ещё 2 соседних оттенка. Красить только в цвет утверждённого выкраса.
2. Краску заказывать по коду из графы «Система и код цвета» у бренда этого кода, не «аналогом» другого; весь объём одного кода — одной партией, колеруемую краску — за один проход машины.
3. Площади — те же, что в ведомости отделки (лист С1); сколько краски заказать — в спецификации отделочных материалов (лист С4).

Схема квартиры: цвет стен и акценты (б/м)


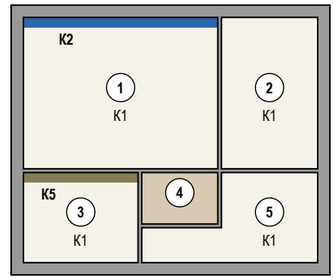


Схема палитры проекта


Стиль: Средиземноморский 60% + Скандинавский 40% · схема: комплементарная

основной	основной	второстепенный	второстепенный	второстепенный	акцентный	акцентный	акцентный
Tikkurila G503	**Little Greene No. 222**	**NCS S 1010-Y20R**	**Farrow & Ball No. 89**	**Farrow & Ball No. 292**	**NCS S 3050-R80B**	**Farrow & Ball No. 66**	**NCS S 5020-G90Y**
Calla LRV 89 стены 1,2,3,5; плинтус 1,2,3,5	Loft White LRV 92 потолок 1,2,3,4,5; текстиль/декор 1,3	Светлый песок / известняк LRV 75 текстиль/декор 1,3	Lulworth Blue — светлая морская лазурь LRV ≈45 в отделке не применён	Treron — серо-оливковая листва LRV 15 в отделке не применён	Эгейский синий LRV ≈13 акцент 1; текстиль/декор 1	India Yellow – охра / горчица итальянских фасадов LRV 36 в отделке не применён	Олива LRV ≈20 акцент 3; текстиль/декор 3

План 60/30/10

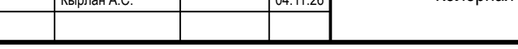

Окраска, факт — по площади стен, акцентов, потолков

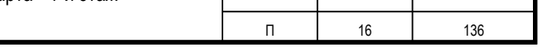

окрашено всего 238,5 м²; второстепенный тон несут мебель и текстиль

Текстиль и декор в цветах вне палитры проекта

Tikkurila X463 X463 Sandstone — песчаник — пом. 1 (T15, T16, T19), 3 (T9)

Условные обозначения

- **K1** Tikkurila G503 · Calla · краска · матовая · кл. 1
- **K2** NCS S 3050-R80B · Эгейский синий · Tikkurila · матовая · кл. 1
- **K3** Little Greene No. 222 · Loft White · Absolute Matt · глубокомат. · кл. 2
- **K4** Tikkurila G503 · Calla · МДФ
- **K5** NCS S 5020-G90Y · Олива · Tikkurila · матовая · кл. 1
- **K6** Little Greene No. 222 · Loft White · Intelligent Bathroom · матовая · кл. 1
- дерево (доска, паркет, ламинат) — рисунок досок
- керамогранит, плитка, камень — сетка швов по формату
- **KM1** инженерная доска · 1167-4250
- **KM2** аналог: керамогранит под травертин, матовый, 1200×600×9 мм
- **KM3** плитка · A8UZ
- **KM4** аналог: керамогранит ректифицированный под травертин, матовый, 600×600×9 мм
- **KM5** керамогранит · A8UZ

K — краска, KM — отделочный материал (тон KM — по описанию, эталон — образец материала); кл. — класс истирания (1 — самый стойкий к мытью); LRV — светлота цвета: 0 — чёрный, 100 — белый; «≈» — ориентировочно

					Проект: Дом 120 м²
	Лист	№ док.	Подпись	Дата	
Дизайнер	Кырлан А.С.			04.11.26	Колерная карта · 1-й этаж
					Стадия: П; Лист: 16; Листов: 136

Колерная карта по помещениям

Помещение	Поверхность	Образец	Поз.	Система и код цвета	Производитель, линейка / материал, артикул	Блеск	Класс истирания	LRV	Площадь
6. Спальня родителей 17,17 м²	стены		**K1**	Tikkurila G503	Tikkurila	матовая	1	89	32,6 м²
	акцент А		**K2**	Farrow & Ball No. 89	Farrow & Ball · Modern Emulsion	матовая	1	≈45	7,2 м²
	потолок		**K3**	Little Greene No. 222	Little Greene · Absolute Matt	глубокомат.	2	92	17,2 м²
	пол		**KM1**	по образцу	Coswick · Вековые традиции · арт. 1167-4250				17,2 м²
	плинтус		**K4**	Tikkurila G503	МДФ · в цвет Tikkurila			89	15,9 м
7. Детская 12,3 м²	стены		**K5**	Tikkurila G503	Tikkurila	полуматов.	1	89	24,0 м²
	акцент А		**K6**	Farrow & Ball No. 66	Farrow & Ball	полуматов.	1	36	10,1 м²
	потолок		**K3**	Little Greene No. 222	Little Greene · Absolute Matt	глубокомат.	2	92	12,3 м²
	пол		**KM1**	по образцу	Coswick · Вековые традиции · арт. 1167-4250				12,3 м²
	плинтус		**K7**	Tikkurila G503	Orac Decor · Contour (Luxxus)			89	13,3 м
8. Гардеробная 3,82 м²	стены		**K8**	Little Greene No. 222	Little Greene · Intelligent Matt	матовая	1	92	22,1 м²
	потолок		**K3**	Little Greene No. 222	Little Greene · Absolute Matt	глубокомат.	2	92	3,8 м²
	пол		**KM1**	по образцу	Coswick · Вековые традиции · арт. 1167-4250				3,8 м²
	плинтус		**K9**	Little Greene No. 222	МДФ · в цвет Little Greene			92	7,4 м
9. Кладовая 4,66 м²	стены		**K10**	NCS S 0502-Y	Tikkurila	матовая	2	86	23,6 м²
	потолок		**K11**	NCS S 0300-N	Tikkurila	глубокомат.	2	92	4,7 м²
	пол		**KM1**	по образцу	Coswick · Вековые традиции · арт. 1167-4250				4,7 м²
	плинтус		**K12**	NCS S 0300-N	Orac Decor · Contour (Luxxus)	полуматов.		92	7,9 м
10. Холл второго этажа 15,51 м²	стены		**K1**	Tikkurila G503	Tikkurila	матовая	1	89	36,8 м²
	потолок		**K3**	Little Greene No. 222	Little Greene · Absolute Matt	глубокомат.	2	92	15,5 м²
	пол		**KM1**	по образцу	Coswick · Вековые традиции · арт. 1167-4250				15,5 м²
	плинтус		**K4**	Tikkurila G503	МДФ · в цвет Tikkurila			89	12,9 м
11. Коридор второго этажа 5,16 м²	стены		**K1**	Tikkurila G503	Tikkurila	матовая	1	89	17,9 м²
	потолок		**K3**	Little Greene No. 222	Little Greene · Absolute Matt	глубокомат.	2	92	5,2 м²
	пол		**KM1**	по образцу	Coswick · Вековые традиции · арт. 1167-4250				5,2 м²
	плинтус		**K4**	Tikkurila G503	МДФ · в цвет Tikkurila			89	5,7 м
12. Детская вторая 9,23 м²	стены		**K5**	Tikkurila G503	Tikkurila	полуматов.	1	89	22,3 м²
	акцент А		**K13**	Tikkurila H440	Tikkurila	полуматов.	1	≈51	6,8 м²
	потолок		**K3**	Little Greene No. 222	Little Greene · Absolute Matt	глубокомат.	2	92	9,2 м²
	пол		**KM1**	по образцу	Coswick · Вековые традиции · арт. 1167-4250				9,2 м²
	плинтус		**K7**	Tikkurila G503	Orac Decor · Contour (Luxxus)			89	11,4 м
13. Санузел второго этажа 5,31 м²	стены		**KM2**	Marvel Travertine	Atlas Concorde · арт. A8UZ				20,7 м²
	потолок		**K14**	Little Greene No. 222	Little Greene · Intelligent Bathroom	матовая	1	92	5,3 м²
	пол		**KM3**	по образцу	керамогранит · аналог по хар.				5,3 м²

Примечания

1. Цвет на листе и на экране — ориентир. До покраски — выкрас на объекте: не меньше А3 (или лист ГКЛ), на грунте под эту краску, не на белой шпаклёвке, в 2 слоя; на обороте — код, бренд, веер, дата. Смотреть днём и вечером, рядом с образцами пола и плитки; к основному цвету стен — ещё 2 соседних оттенка. Красить только в цвет утверждённого выкраса.
2. Краску заказывать по коду из графы «Система и код цвета» у бренда этого кода, не «аналогом» другого; весь объём одного кода — одной партией, колеруемую краску — за один проход машины.
3. Площади — те же, что в ведомости отделки (лист С1); сколько краски заказать — в спецификации отделочных материалов (лист С4).

Схема палитры проекта


Стиль: Средиземноморский 60% + Скандинавский 40% · схема: комплементарная

основной	основной	второстепенный	второстепенный	второстепенный	акцентный	акцентный	акцентный
Tikkurila G503	**Little Greene No. 222**	**NCS S 1010-Y20R**	**Farrow & Ball No. 89**	**Farrow & Ball No. 292**	**NCS S 3050-R80B**	**Farrow & Ball No. 66**	**NCS S 5020-G90Y**
Calla LRV 89 стены 6,7,10,11,12; плинтус 6,7,10,11,12	Loft White LRV 92 потолок 6,7,8,10,11,12,13; стены 8; плинтус 8; текстиль/декор 6,7,12	Светлый песок / известняк LRV 75 текстиль/декор 6,7,12	Lulworth Blue — светлая морская лазурь LRV ≈45 акцент 6; текстиль/декор 6	Treron — серо-оливковая листва LRV 15 в отделке не применён	Эгейский синий LRV ≈13 в отделке не применён	India Yellow – охра / горчица итальянских фасадов LRV 36 акцент 7; текстиль/декор 7	Олива LRV ≈20 в отделке не применён

План 60/30/10



Окраска, факт — по площади стен, акцентов, потолков

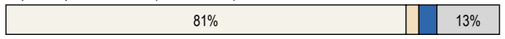

окрашено всего 276,6 м²; серым — цвета вне палитры; второстепенный тон несут мебель и текстиль

Текстиль и декор в цветах вне палитры проекта

- Tikkurila X395 X395 Playa — влажный пляжный песок — пом. 6 (Т3)
- Tikkurila X463 X463 Sandstone — песчаник — пом. 7 (Т22), 12 (Т28)

Условные обозначения

- **K1** Tikkurila G503 · Calla · краска · матовая · кл. 1
- **K2** Farrow & Ball No. 89 · Lulworth Blue — светлая морская лазурь · Modern Emulsion · матовая · кл. 1
- **K3** Little Greene No. 222 · Loft White · Absolute Matt · глубокомат. · кл. 2
- **K4** Tikkurila G503 · Calla · МДФ
- **K5** Tikkurila G503 · Calla · краска · полуматов. · кл. 1
- **K6** Farrow & Ball No. 66 · India Yellow — охра / горчица итальянских фасадов · краска · полуматов. · кл. 1
- **K7** Tikkurila G503 · Calla · Contour (Luxxus)
- **K8** Little Greene No. 222 · Loft White · Intelligent Matt · матовая · кл. 1
- **K9** Little Greene No. 222 · Loft White · МДФ
- дерево (доска, паркет, ламинат) — рисунок досок
- керамогранит, плитка, камень — сетка швов по формату
- плашка не залита — цвет только по коду и вееру бренда
- **K10** NCS S 0502-Y · Tikkurila · матовая · кл. 2
- **K11** NCS S 0300-N · Tikkurila · глубокомат. · кл. 2
- **K12** NCS S 0300-N · Orac Decor Contour (Luxxus) · полуматов.
- **K13** Tikkurila H440 · H440 Wave — бирюзово-голубая вода · краска · полуматов. · кл. 1
- **K14** Little Greene No. 222 · Loft White · Intelligent Bathroom · матовая · кл. 1
- **KM1** инженерная доска · 1167-4250
- **KM2** плитка · A8UZ
- **KM3** аналог: керамогранит ректифицированный под травертин, матовый, 600×600×9 мм

К — краска, КМ — отделочный материал (тон КМ — по описанию, эталон — образец материала); кл. — класс истирания (1 — самый стойкий к мытью); LRV — светлота цвета: 0 — чёрный, 100 — белый; «≈» — ориентировочно

Перечень выкрасов на согласование

№	Код	Бренд / веер	Пом. / стена	Подложка	Формат	Статус
1	G503	Tikkurila	6, 7, 10, 11, 12	ГКЛ с грунтом; МДФ под эмаль	600×1000; 300×600	к выполнению

… ещё 6 выкрасов — в ведомости отделки

					Проект: Дом 120 м²			
	Лист	№ док.	Подпись	Дата	Колерная карта · 2-й этаж	Стадия	Лист	Листов
Дизайнер	Кырлан А.С.			04.11.26		П	17	136

выпуск 04.11.2026 № 406ed8a6ce · стр. 17 из 136

Колерная карта по помещениям (продолжение)

Помещение	Поверхность	Образец	Поз.	Система и код цвета	Производитель, линейка / материал, артикул	Блеск	Класс истирания	LRV	Площадь
7. Детская 12,3 м²	стены		**K8**	Tikkurila G503	Tikkurila	полуматов.	1	89	24,0 м²
	акцент А		**K9**	Farrow & Ball No. 66	Farrow & Ball	полуматов.	1	36	10,1 м²
	потолок		**K3**	Little Greene No. 222	Little Greene · Absolute Matt	глубокомат.	2	92	12,3 м²
	пол		**KM1**	по образцу	Coswick · Вековые традиции · арт. 1167-4250				12,3 м²
	плинтус		**K10**	Tikkurila G503	Orac Decor · Contour (Luxxus)			89	13,3 м
8. Гардеробная 3,82 м²	стены		**K11**	Little Greene No. 222	Little Greene · Intelligent Matt	матовая	1	92	22,1 м²
	потолок		**K3**	Little Greene No. 222	Little Greene · Absolute Matt	глубокомат.	2	92	3,8 м²
	пол		**KM1**	по образцу	Coswick · Вековые традиции · арт. 1167-4250				3,8 м²
	плинтус		**K12**	Little Greene No. 222	МДФ · в цвет Little Greene			92	7,4 м
9. Кладовая 4,66 м²	стены		**K13**	NCS S 0502-Y	Tikkurila	матовая	2	86	23,6 м²
	потолок		**K14**	NCS S 0300-N	Tikkurila	глубокомат.	2	92	4,7 м²
	пол		**KM1**	по образцу	Coswick · Вековые традиции · арт. 1167-4250				4,7 м²
	плинтус		**K15**	NCS S 0300-N	Orac Decor · Contour (Luxxus)	полуматов.		92	7,9 м
10. Холл второго этажа 15,51 м²	стены		**K1**	Tikkurila G503	Tikkurila	матовая	1	89	33,0 м²
	потолок		**K3**	Little Greene No. 222	Little Greene · Absolute Matt	глубокомат.	2	92	15,5 м²
	пол		**KM1**	по образцу	Coswick · Вековые традиции · арт. 1167-4250				15,5 м²
	плинтус		**K4**	Tikkurila G503	МДФ · в цвет Tikkurila			89	11,1 м
11. Коридор второго этажа 5,16 м²	стены		**K1**	Tikkurila G503	Tikkurila	матовая	1	89	17,9 м²
	потолок		**K3**	Little Greene No. 222	Little Greene · Absolute Matt	глубокомат.	2	92	5,2 м²
	пол		**KM1**	по образцу	Coswick · Вековые традиции · арт. 1167-4250				5,2 м²
	плинтус		**K4**	Tikkurila G503	МДФ · в цвет Tikkurila			89	5,7 м
12. Детская вторая 9,23 м²	стены		**K8**	Tikkurila G503	Tikkurila	полуматов.	1	89	22,3 м²
	акцент А		**K16**	Tikkurila H440	Tikkurila	полуматов.	1	≈51	6,8 м²
	потолок		**K3**	Little Greene No. 222	Little Greene · Absolute Matt	глубокомат.	2	92	9,2 м²
	пол		**KM1**	по образцу	Coswick · Вековые традиции · арт. 1167-4250				9,2 м²
	плинтус		**K10**	Tikkurila G503	Orac Decor · Contour (Luxxus)			89	11,4 м
13. Санузел второго этажа 5,31 м²	стены		**KM3**	Marvel Travertine	Atlas Concorde · арт. A8UZ				19,1 м²
	потолок		**K6**	Little Greene No. 222	Little Greene · Intelligent Bathroom	матовая	1	92	5,3 м²
	пол		**KM4**	по образцу	керамогранит · аналог по хар.				5,3 м²

Условные обозначения

- **K1** Tikkurila G503 · Calla · краска · матовая · кл. 1
- **K2** NCS S 3050-R80B · Эгейский синий · Tikkurila · матовая · кл. 1
- **K3** Little Greene No. 222 · Loft White · Absolute Matt · глубокомат. · кл. 2
- **K4** Tikkurila G503 · Calla · МДФ
- **K5** NCS S 5020-G90Y · Олива · Tikkurila · матовая · кл. 1
- **K6** Little Greene No. 222 · Loft White · Intelligent Bathroom · матовая · кл. 1
- **K7** Farrow & Ball No. 89 · Lulworth Blue — светлая морская лазурь · Modern Emulsion · матовая · кл. 1
- **K8** Tikkurila G503 · Calla · краска · полуматов. · кл. 1
- **K9** Farrow & Ball No. 66 · India Yellow — охра / горчица итальянских фасадов · краска · полуматов. · кл. 1
- **K10** Tikkurila G503 · Calla · Contour (Luxxus)
- **K11** Little Greene No. 222 · Loft White · Intelligent Matt · матовая · кл. 1
- **K12** Little Greene No. 222 · Loft White · МДФ
- **K13** NCS S 0502-Y · Tikkurila · матовая · кл. 2
- **K14** NCS S 0300-N · Tikkurila · глубокомат. · кл. 2
- **K15** NCS S 0300-N · Orac Decor Contour (Luxxus) · полуматов.
- **K16** Tikkurila H440 · H440 Wave — бирюзово-голубая вода · краска · полуматов. · кл. 1
- **KM1** инженерная доска · 1167-4250
- **KM2** аналог: керамогранит под травертин, матовый, 1200×600×9 мм
- **KM3** плитка · A8UZ
- **KM4** аналог: керамогранит ректифицированный под травертин, матовый, 600×600×9 мм
- **KM5** керамогранит · A8UZ

дерево (доска, паркет, ламинат) — рисунок досок

керамогранит, плитка, камень — сетка швов по формату

плашка не залита — цвет только по коду и вееру бренда

K — краска, KM — отделочный материал (тон KM — по описанию, эталон — образец материала); кл. — класс истирания (1 — самый стойкий к мытью); LRV — светлота цвета: 0 — чёрный, 100 — белый; «≈» — ориентировочно

Перечень выкрасов на согласование


№	Код	Бренд / веер	Пом. / стена	Подложка	Формат	Статус
1	G503	Tikkurila	1, 2, 3, 5, 6, 7, 10, 11, 12	ГКЛ с грунтом; МДФ под эмаль	600×1000; 300×600	к выполнению
2	S 3050-R80B	NCS Tikkurila	1 A	ГКЛ с грунтом	600×1000	к выполнению
3	No. 222	Little Greene	1, 2, 3, 4, 5, 6, 7, 8, 10, 11, 12, 13	ГКЛ с грунтом; МДФ под эмаль	600×1000; 300×600	к выполнению
4	S 5020-G90Y	NCS Tikkurila	3 A	ГКЛ с грунтом	600×1000	к выполнению
5	No. 89	Farrow & Ball	6 A	ГКЛ с грунтом	600×1000	к выполнению
6	No. 66	Farrow & Ball	7 A	ГКЛ с грунтом	600×1000	к выполнению
7	S 0502-Y	NCS Tikkurila	9	ГКЛ с грунтом	600×1000	к выполнению
8	S 0300-N	NCS Tikkurila	9	ГКЛ с грунтом; МДФ под эмаль	600×1000; 300×600	к выполнению
9	H440	Tikkurila	12 A	ГКЛ с грунтом	600×1000	к выполнению

Примечания

1. Цвет на листе и на экране — ориентир. До покраски — выкрас на объекте: не меньше А3 (или лист ГКЛ), на грунте под эту краску, не на белой шпаклёвке, в 2 слоя; на обороте — код, бренд, веер, дата. Смотреть днём и вечером, рядом с образцами пола и плитки; к основному цвету стен — ещё 2 соседних оттенка. Красить только в цвет утверждённого выкраса.
2. Краску заказывать по коду из графы «Система и код цвета» у бренда этого кода, не «аналогом» другого; весь объём одного кода — одной партией, колеруемую краску — за один проход машины.
3. Площади — те же, что в ведомости отделки (лист С1); сколько краски заказать — в спецификации отделочных материалов (лист С4).
4. Колерная карта на 2 листах: обозначения — на каждом, схема и палитра — на первом, выкрасы — на последнем.

					Проект: Дом 120 м²
	Лист	№ док.	Подпись	Дата	
Дизайнер	Кырлан А.С.			04.11.26	Колерная карта

Стадия	Лист	Листов
П	18	136

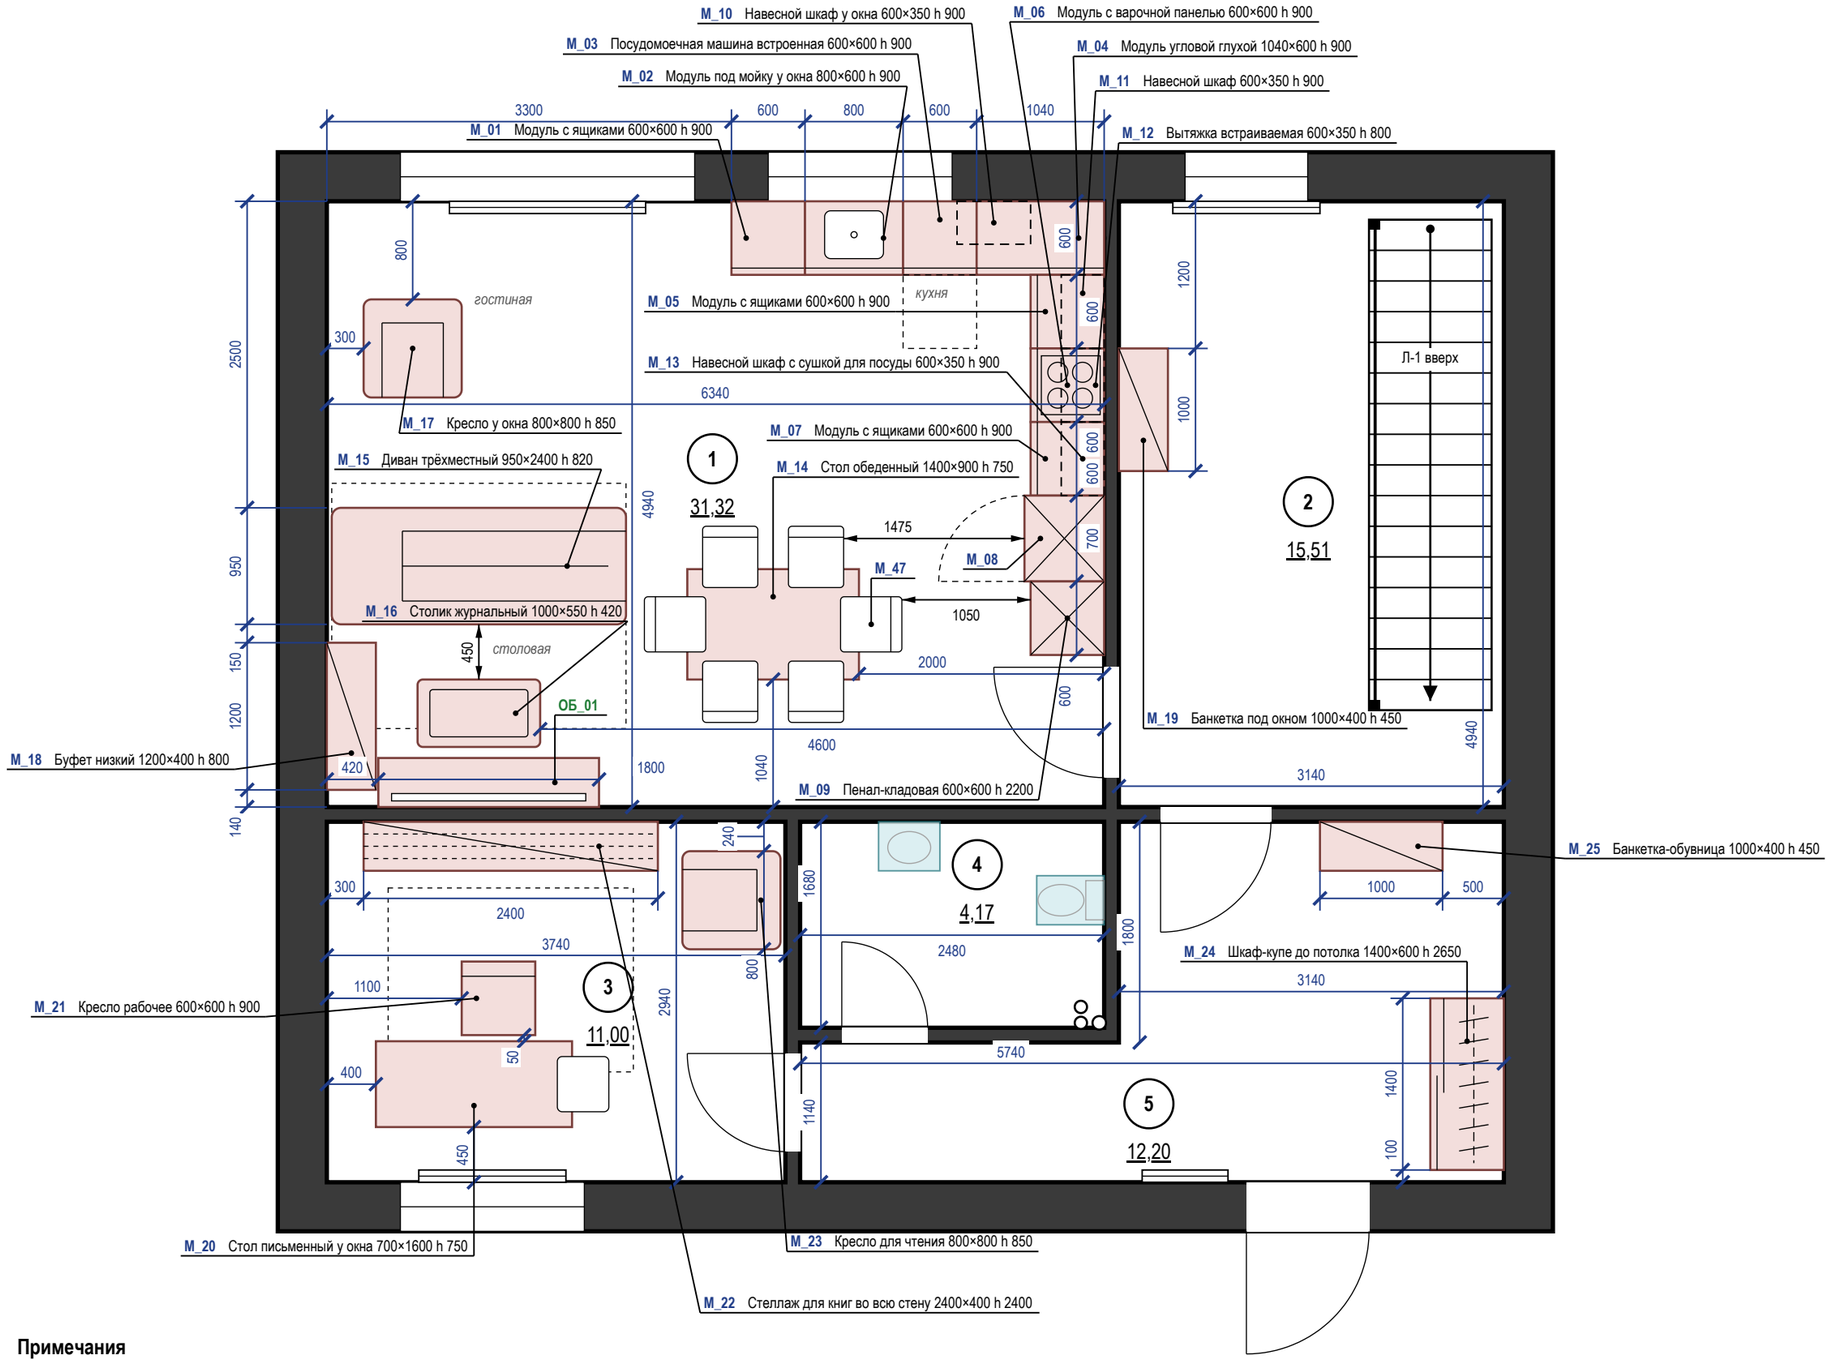

Экспликация помещений

лист 6 · на плане — номера в марках

Ведомость мебели и оборудования

Марка	Наименование	Ш×Г×В, мм	Пом.	Кол.
M_01	Модуль с ящиками	600×600×900	1	1
M_02	Модуль под мойку у окна	800×600×900	1	1
M_03	Посудомоечная машина встроенная	600×600×900	1	1
M_04	Модуль угловой глухой	1040×600×900	1	1
M_05	Модуль с ящиками	600×600×900	1	1
M_06	Модуль с варочной панелью	600×600×900	1	1
M_07	Модуль с ящиками	600×600×900	1	1
M_08	Колонна с холодильником	700×650×2200	1	1
M_09	Пенал-кладовая	600×600×2200	1	1
M_10	Навесной шкаф у окна	600×350×900	1	1
M_11	Навесной шкаф	600×350×900	1	1
M_12	Вытяжка встраиваемая	600×350×800	1	1
M_13	Навесной шкаф с сушкой для посуды	600×350×900	1	1
M_14	Стол обеденный 1400×900	1400×900×750	1	1
ОБ_01	ТВ-тумба подвесная с экраном	1800×400×600	1	1
M_15	Диван трёхместный	950×2400×820	1	1
M_16	Столик журнальный	1000×550×420	1	1
M_17	Кресло у окна	800×800×850	1	1
M_18	Буфет низкий	1200×400×800	1	1
M_19	Банкетка под окном	1000×400×450	2	1
M_20	Стол письменный у окна	700×1600×750	3	1
M_21	Кресло рабочее	600×600×900	3	1
M_22	Стеллаж для книг во всю стену	2400×400×2400	3	1
M_23	Кресло для чтения	800×800×850	3	1
M_24	Шкаф-купе до потолка	1400×600×2650	5	1
M_25	Банкетка-обувница	1000×400×450	5	1
M_47	Стул обеденный к столу M_14	450×500×820	1	6

Ш — вдоль стены (изголовья), Г — от стены (длина кровати)


Материалы, модели, допуск замены — лист 21

Примечания

1. Размеры — в мм от чистовых поверхностей стен; размеры мебели уточнить после отделочных работ; общие указания — лист 3.
2. Отступ от стены, на плане не образмерен: M_15 — 40 мм, M_23 — 40 мм.
3. У позиций M_08, ОБ_01, M_47 на плане только марка: наименование и габарит — в спецификации, лист 21.
4. Стулья обеденной группы (M_47 — 6 шт.) показаны в рабочем положении, задвинутыми под столешницу на 150 мм.

					Проект: Дом 120 м²	M 1:50
	Лист	№ док.	Подпись	Дата	План размещения мебели и оборудования · 1-й этаж	Стадия / Лист / Листов
Дизайнер	Кырлан А.С.			04.11.26		П / 19 / 136

выпуск 04.11.2026 № 406ed8a6ce · стр. 19 из 136

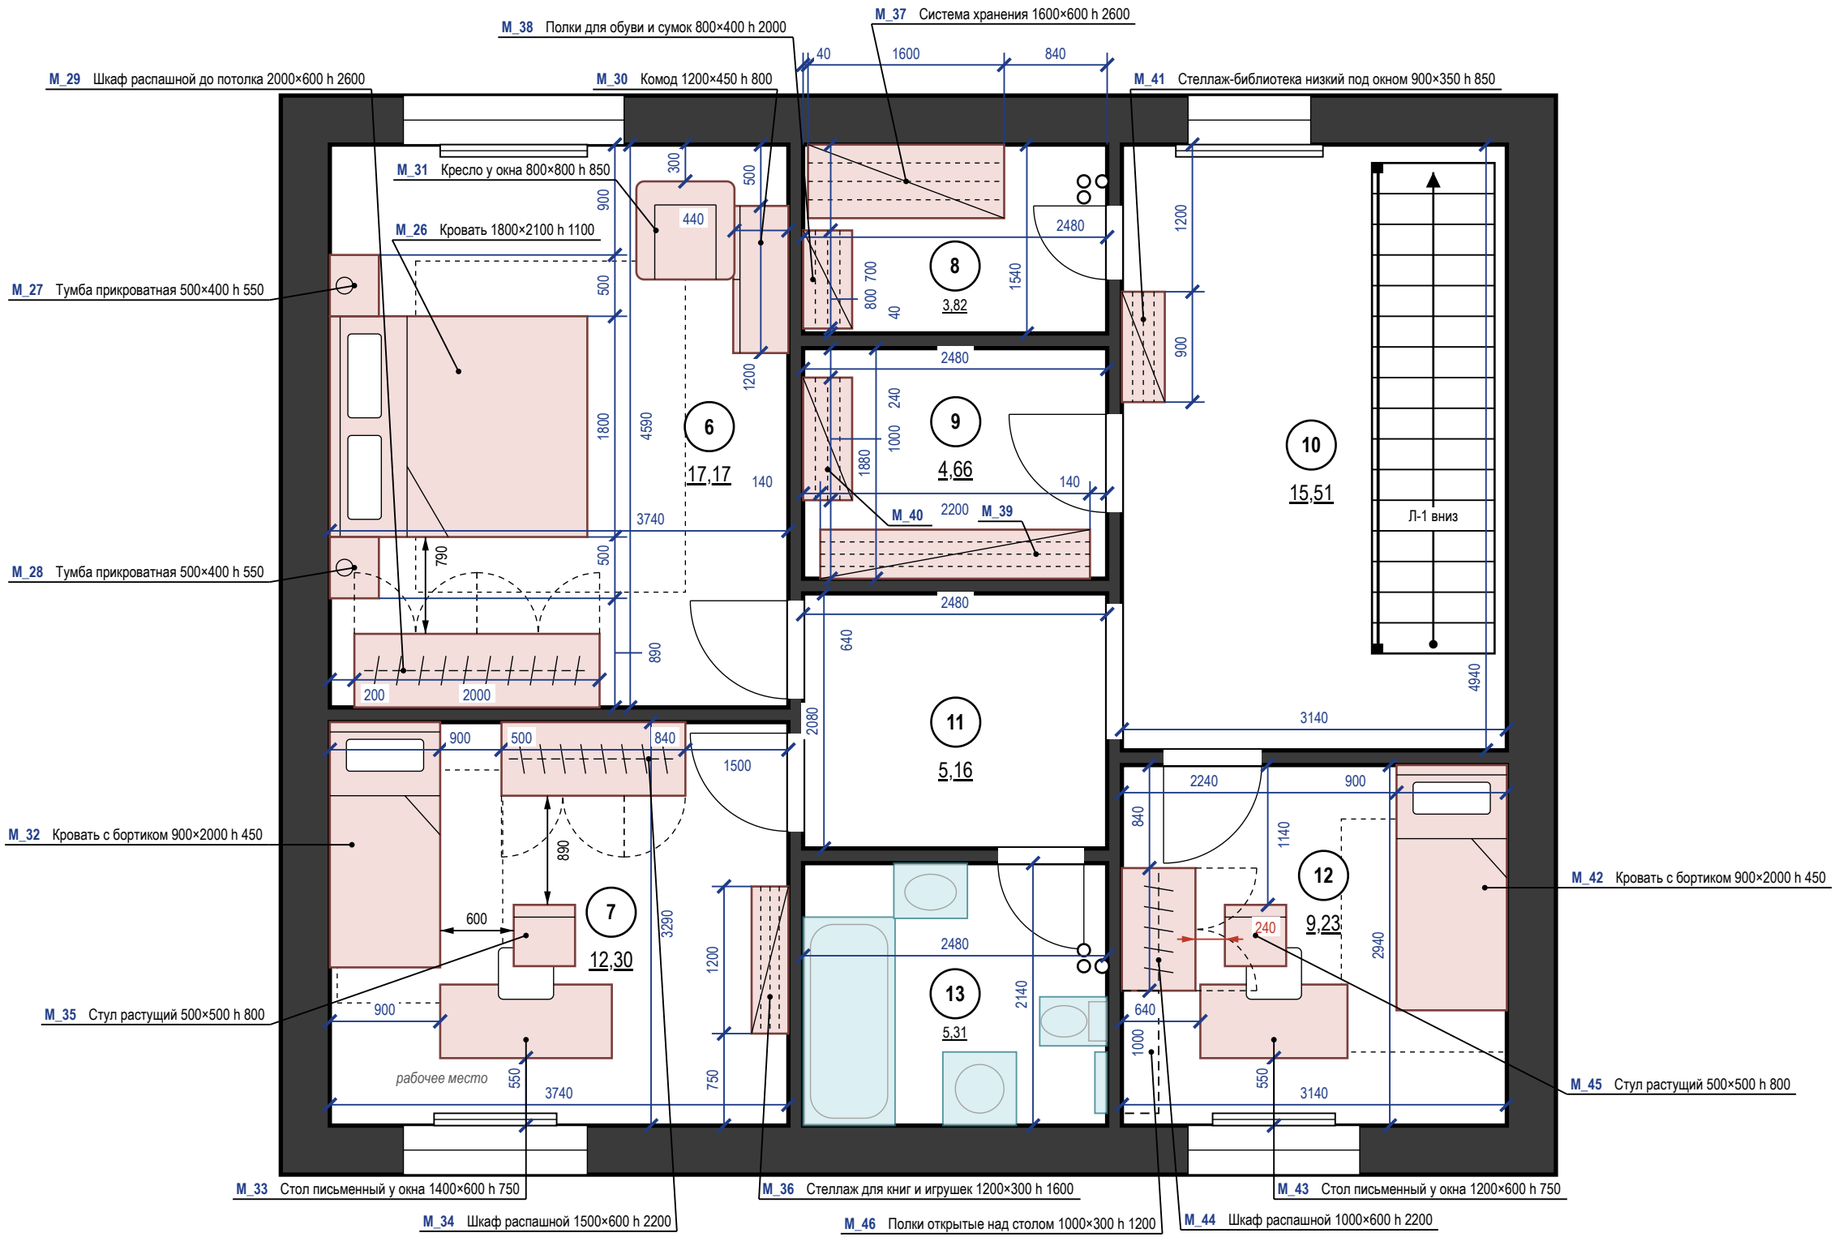

Экспликация помещений

лист 7 · на плане — номера в марках

Ведомость мебели и оборудования

Марка	Наименование	Ш×Г×В, мм	Пом.	Кол.
M_26	Кровать 1800×2000	1800×2100×1100	6	1
M_27	Тумба прикроватная	500×400×550	6	1
M_28	Тумба прикроватная	500×400×550	6	1
M_29	Шкаф распашной до потолка	2000×600×2600	6	1
M_30	Комод	1200×450×800	6	1
M_31	Кресло у окна	800×800×850	6	1
M_32	Кровать 900×2000 с бортиком	900×2000×450	7	1
M_33	Стол письменный у окна	1400×600×750	7	1
M_34	Шкаф распашной	1500×600×2200	7	1
M_35	Стул растущий	500×500×800	7	1
M_36	Стеллаж для книг и игрушек	1200×300×1600	7	1
M_37	Система хранения	1600×600×2600	8	1
M_38	Полки для обуви и сумок	800×400×2000	8	1
M_39	Стеллаж для хранения	2200×400×2200	9	1
M_40	Стеллаж узкий для бытовой техники	1000×400×2200	9	1
M_41	Стеллаж-библиотека низкий под окном	900×350×850	10	1
M_42	Кровать 900×2000 с бортиком	900×2000×450	12	1
M_43	Стол письменный у окна	1200×600×750	12	1
M_44	Шкаф распашной	1000×600×2200	12	1
M_45	Стул растущий	500×500×800	12	1
M_46	Полки открытые над столом	1000×300×1200	12	1

Ш — вдоль стены (изголовья), Г — от стены (длина кровати)

Материалы, модели, допуск замены — лист 21

Примечания

1. Размеры — в мм от чистовых поверхностей стен; размеры мебели уточнить после отделочных работ; общие указания — лист 3.
2. У позиций M_39, M_40 на плане только марка: наименование и габарит — в спецификации, лист 21.

	Лист	№ док.	Подпись	Дата	
Дизайнер	Кырлан А.С.			04.11.26	Проект: Дом 120 м² — **М 1:50**
					План размещения мебели и оборудования · 2-й этаж

Стадия	Лист	Листов
П	20	136

Поз.	Наименование и техническая характеристика	Тип, марка, обозначение документа, опросного листа	Код продукции	Поставщик	Ед. измерения	Кол.	Масса 1 ед., кг	Примечание
	Мебель встроенная и корпусная (изготовление по чертежам мебельщика)							
M_01	Модуль с ящиками; корпус ЛДСП 16 мм; фасады — МДФ 18 мм, эмаль матовая; цвет фасадов — в цвет стен (Tikkurila G503); Ш×Г×В 600×600×900 мм			изготовление на заказ	шт.	1		пом. 1
M_02	Модуль под мойку у окна; корпус ЛДСП 16 мм; фасады — МДФ 18 мм, эмаль матовая; цвет фасадов — в цвет стен (Tikkurila G503); Ш×Г×В 800×600×900 мм			изготовление на заказ	шт.	1		пом. 1
M_03	Модуль под встраиваемую ПММ 60; без корпуса (ниша между соседними модулями); фасад на дверь машины — МДФ 18 мм, эмаль матовая; цоколь; цвет фасадов — в цвет стен (Tikkurila G503); Ш×Г×В 600×600×900 мм			изготовление на заказ	шт.	1		пом. 1
M_04	Модуль угловой глухой, поворотные полки; корпус ЛДСП 16 мм; фасады — МДФ 18 мм, эмаль матовая; цвет фасадов — в цвет стен (Tikkurila G503); Ш×Г×В 1040×600×900 мм			изготовление на заказ	шт.	1		пом. 1
M_05	Модуль с ящиками; корпус ЛДСП 16 мм; фасады — МДФ 18 мм, эмаль матовая; цвет фасадов — в цвет стен (Tikkurila G503); Ш×Г×В 600×600×900 мм			изготовление на заказ	шт.	1		пом. 1
M_06	Модуль с варочной панелью и духовым шкафом; корпус ЛДСП 16 мм; фасады — МДФ 18 мм, эмаль матовая; цвет фасадов в цвет стен (Tikkurila G503); Ш×Г×В 600×600×900 мм			изготовление на заказ	шт.	1		пом. 1
M_07	Модуль с ящиками; корпус ЛДСП 16 мм; фасады — МДФ 18 мм, эмаль матовая; цвет фасадов — в цвет стен (Tikkurila G503); Ш×Г×В 600×600×900 мм			изготовление на заказ	шт.	1		пом. 1
M_08	Колонна с холодильником; корпус ЛДСП 16 мм; фасады — МДФ 18 мм, эмаль матовая; цвет фасадов — в цвет стен (Tikkurila G503); Ш×Г×В 700×650×2200 мм			изготовление на заказ	шт.	1		пом. 1
M_09	Пенал-кладовая с выдвижными корзинами; корпус ЛДСП 16 мм; фасады — МДФ 18 мм, эмаль матовая; цвет фасадов — в цвет стен (Tikkurila G503); Ш×Г×В 600×600×2200 мм			изготовление на заказ	шт.	1		пом. 1
M_10	Навесной шкаф у окна, витрина со стеклом; корпус ЛДСП 16 мм; фасады — МДФ 18 мм, эмаль матовая; цвет фасадов — в цвет стен (Tikkurila G503); Ш×Г×В 600×350×900 мм			изготовление на заказ	шт.	1		пом. 1
M_11	Навесной шкаф, фасад в тон цоколя; корпус ЛДСП 16 мм; фасады — МДФ 18 мм, эмаль матовая; цвет фасадов — в цвет стен (Tikkurila G503); Ш×Г×В 600×350×900 мм			изготовление на заказ	шт.	1		пом. 1
M_12	Вытяжка встраиваемая в навесной шкаф; корпус ЛДСП 16 мм; фасады — МДФ 18 мм, эмаль матовая; цвет фасадов — в цвет стен (Tikkurila G503); Ш×Г×В 600×350×800 мм			изготовление на заказ	шт.	1		пом. 1
M_13	Навесной шкаф с сушкой для посуды; корпус ЛДСП 16 мм; фасады — МДФ 18 мм, эмаль матовая; цвет фасадов — в цвет стен (Tikkurila G503); Ш×Г×В 600×350×900 мм			изготовление на заказ	шт.	1		пом. 1
M_24	Шкаф-купе до потолка, дуб табак, планка-компенсатор до подшивки; корпус ЛДСП 16 мм; фасады — ЛДСП 10 мм в алюминиевом профиле; Ш×Г×В 1400×600×2650 мм			изготовление на заказ	шт.	1		пом. 5
M_29	Шкаф распашной до потолка, фасады матовые; корпус ЛДСП 16 мм; фасады — МДФ 18 мм, эмаль матовая; цвет фасадов в цвет стен (Tikkurila G503); Ш×Г×В 2000×600×2600 мм			изготовление на заказ	шт.	1		пом. 6
M_34	Шкаф распашной; корпус ЛДСП 16 мм; фасады — МДФ 18 мм, эмаль матовая; цвет фасадов — в цвет стен (Tikkurila G503); Ш×Г×В 1500×600×2200 мм			изготовление на заказ	шт.	1		пом. 7
M_37	Система хранения: штанги, полки, ящики; каркас и полки — ЛДСП 16 мм, декор «дуб натуральный»; без фасадов; Ш×Г×В 1600×600×2600 мм			изготовление на заказ	шт.	1		пом. 8; крепление к стене
M_38	Полки для обуви и сумок; каркас и полки — ЛДСП 16 мм, декор «дуб натуральный»; без фасадов; Ш×Г×В 800×400×2000 мм			изготовление на заказ	шт.	1		пом. 8; крепление к стене
M_39	Стеллаж для хранения; каркас и полки — ЛДСП 16 мм, декор «дуб натуральный»; без фасадов; Ш×Г×В 2200×400×2200 мм			изготовление на заказ	шт.	1		пом. 9; крепление к стене
M_40	Стеллаж узкий для бытовой техники; каркас и полки — ЛДСП 16 мм, декор «дуб натуральный»; без фасадов; Ш×Г×В 1000×400×2200 мм			изготовление на заказ	шт.	1		пом. 9; крепление к стене
M_44	Шкаф распашной; корпус ЛДСП 16 мм; фасады — МДФ 18 мм, эмаль матовая; цвет фасадов — в цвет стен (Tikkurila G503); Ш×Г×В 1000×600×2200 мм			изготовление на заказ	шт.	1		пом. 12
M_46	Полки открытые над столом; каркас и полки — ЛДСП 16 мм, декор «дуб натуральный»; без фасадов; Ш×Г×В 1000×300×1200 мм			изготовление на заказ	шт.	1		пом. 12; крепление к стене

Примечания

1. Позиции мебели совпадают с марками на плане расстановки; размеры Ш×Г×В — Ш вдоль стены, Г от стены.
2. Размеры и привязки плана расстановки — в мм от чистовых поверхностей стен: слой штукатурки 20 мм по блоку и 5 мм шпаклёвки по ГКЛ учтён; привязки — от стен и углов помещения, а не от другой мебели.
3. План расстановки не является документацией для изготовления мебели. Встроенная и корпусная мебель изготавливается по чертежам мебельщика после контрольного обмера (после штукатурки); «стена в стену» — с зазором 10 мм с каждой стороны или с компенсаторами; графы «Тип, марка» и «Код продукции» для неё не заполняются (ГОСТ 21.110-2013).
4. Покупные изделия — аналог по характеристикам: заменять только на изделия не больше указанного габарита и того же материала и цвета.
5. Материал и цвет, не указанные в данных изделия, приняты по концепции: тон дерева — по полу, обивка — по вторичному цвету палитры; образцы согласовать до заказа.
6. Масса 1 ед. для изделий до 25 кг не указывается. Техника — по монтажным схемам изготовителя; выводы — по листам ЭОМ и ВК.

					Проект: Дом 120 м²
	Лист	№ док.	Подпись	Дата	Спецификация мебели и оборудования
Дизайнер	Кырлан А.С.			04.11.26	

Стадия	Лист	Листов
П	21	136

Поз.	Наименование и техническая характеристика	Тип, марка, обозначение документа, опросного листа	Код продукции	Поставщик	Ед. измерения	Кол.	Масса 1 ед., кг	Примечание
	Мебель покупная							
M_14	Стол обеденный 1400×900, дуб табак; шпон, дуб натуральный, матовое масло; Ш×Г×В 1400×900×750 мм			аналог по характеристикам	шт.	1		пом. 1; замена ≤ габарита
M_15	Диван трёхместный, лён; обивка — ткань, цвет NCS S 1010-Y20R; Ш×Г×В 950×2400×820 мм			аналог по характеристикам	шт.	1		пом. 1; замена ≤ габарита
M_16	Столик журнальный, дуб и латунь; шпон, дуб натуральный, матовое масло; Ш×Г×В 1000×550×420 мм			аналог по характеристикам	шт.	1		пом. 1; замена ≤ габарита
M_17	Кресло у окна, букле; обивка — ткань, цвет NCS S 1010-Y20R; Ш×Г×В 800×800×850 мм			аналог по характеристикам	шт.	1		пом. 1; замена ≤ габарита
M_18	Буфет низкий, дуб табак; шпон, дуб натуральный, матовое масло; Ш×Г×В 1200×400×800 мм			аналог по характеристикам	шт.	1		пом. 1; крепление к стене; замена ≤ габарита
M_47	Стул обеденный к столу M_14; обивка — ткань, цвет NCS S 1010-Y20R; каркас — дуб натуральный; Ш×Г×В 450×500×820 мм			аналог по характеристикам	шт.	6		пом. 1; замена ≤ габарита
ОБ_01	ТВ-тумба подвесная с экраном, дуб табак; шпон, дуб натуральный, матовое масло; Ш×Г×В 1800×400×600 мм			аналог по характеристикам	шт.	1		пом. 1; замена ≤ габарита
M_19	Банкетка под окном, дуб табак; Ш×Г×В 1000×400×450 мм			аналог по характеристикам	шт.	1		пом. 2; замена ≤ габарита
M_20	Стол письменный у окна, дуб табак; шпон, дуб натуральный, матовое масло; Ш×Г×В 700×1600×750 мм			аналог по характеристикам	шт.	1		пом. 3; замена ≤ габарита
M_21	Кресло рабочее; обивка — ткань, цвет NCS S 1010-Y20R; каркас — дуб натуральный; Ш×Г×В 600×600×900 мм			аналог по характеристикам	шт.	1		пом. 3; замена ≤ габарита
M_22	Стеллаж для книг во всю стену; шпон, дуб натуральный, матовое масло; Ш×Г×В 2400×400×2400 мм			аналог по характеристикам	шт.	1		пом. 3; крепление к стене; замена ≤ габарита
M_23	Кресло для чтения; обивка — ткань, цвет NCS S 1010-Y20R; Ш×Г×В 800×800×850 мм			аналог по характеристикам	шт.	1		пом. 3; замена ≤ габарита
M_25	Банкетка-обувница; Ш×Г×В 1000×400×450 мм			аналог по характеристикам	шт.	1		пом. 5; замена ≤ габарита
M_26	Кровать 1800×2000 с мягким изголовьем 1100, лён; мягкое изголовье, обивка — ткань, цвет NCS S 1010-Y20R; Ш×Г×В 1800×2100×1100 мм			аналог по характеристикам	шт.	1		пом. 6; замена ≤ габарита
M_27, M_28	Тумба прикроватная, дуб табак; шпон, дуб натуральный, матовое масло; Ш×Г×В 500×400×550 мм			аналог по характеристикам	шт.	2		пом. 6; замена ≤ габарита
M_30	Комод, дуб табак; шпон, дуб натуральный, матовое масло; Ш×Г×В 1200×450×800 мм			аналог по характеристикам	шт.	1		пом. 6; крепление к стене; замена ≤ габарита
M_31	Кресло у окна; обивка — ткань, цвет NCS S 1010-Y20R; Ш×Г×В 800×800×850 мм			аналог по характеристикам	шт.	1		пом. 6; замена ≤ габарита
M_32, M_42	Кровать 900×2000 с бортиком; мягкое изголовье, обивка — ткань, цвет NCS S 1010-Y20R; Ш×Г×В 900×2000×450 мм			аналог по характеристикам	шт.	2		пом. 7, 12; замена ≤ габарита
M_33	Стол письменный у окна; шпон, дуб натуральный, матовое масло; Ш×Г×В 1400×600×750 мм			аналог по характеристикам	шт.	1		пом. 7; замена ≤ габарита
M_35, M_45	Стул растущий; обивка — ткань, цвет NCS S 1010-Y20R; каркас — дуб натуральный; Ш×Г×В 500×500×800 мм			аналог по характеристикам	шт.	2		пом. 7, 12; замена ≤ габарита
M_36	Стеллаж для книг и игрушек; шпон, дуб натуральный, матовое масло; Ш×Г×В 1200×300×1600 мм			аналог по характеристикам	шт.	1		пом. 7; крепление к стене; замена ≤ габарита
M_41	Стеллаж-библиотека низкий под окном; шпон, дуб натуральный, матовое масло; Ш×Г×В 900×350×850 мм			аналог по характеристикам	шт.	1		пом. 10; крепление к стене; замена ≤ габарита
M_43	Стол письменный у окна; шпон, дуб натуральный, матовое масло; Ш×Г×В 1200×600×750 мм			аналог по характеристикам	шт.	1		пом. 12; замена ≤ габарита
	Техника встраиваемая и бытовая (покупные изделия), светильники под розетки							
	Посудомоечная машина встраиваемая, в модуле M_03; ниша 600 мм	аналог по характеристикам: полновстраиваемая 60 см под фасад, ниша 600 × 862 мм, навеска фасада в комплекте		по выбору заказчика до изготовления мебели	шт.	1		пом. 1; по схеме изготовителя
	Варочная панель встраиваемая, индукционная, в модуле M_06	аналог по характеристикам: индукционная 60 см, вырез 560 × 490 мм по шаблону модели		по выбору заказчика до изготовления мебели	шт.	1		пом. 1; по схеме изготовителя
	Духовой шкаф встраиваемый, в модуле M_06	аналог по характеристикам: 60 см, лицевая панель 595 мм, ниша 560 × 600, глубина ≥ 550 мм, вентиляция за прибором		по выбору заказчика до изготовления мебели	шт.	1		пом. 1; по схеме изготовителя

					Проект: Дом 120 м²
	Лист	№ док.	Подпись	Дата	Спецификация мебели и оборудования (продолжение)
Дизайнер	Кырлан А.С.			04.11.26	

Стадия	Лист	Листов
П	22	136

Поз.	Наименование и техническая характеристика	Тип, марка, обозначение документа, опросного листа	Код продукции	Поставщик	Ед. измерения	Кол.	Масса 1 ед., кг	Примечание
	Холодильник встраиваемый, в модуле M_08	аналог по характеристикам: полновстраиваемый под фасад, ниша 1780 × 560 × 550 мм, вентиляция решётка в цоколе, выход сверху		по выбору заказчика до изготовления мебели	шт.	1		пом. 1; по схеме изготовителя
	Вытяжка встраиваемая, в модуле M_12	аналог по характеристикам: производительность — по расчёту ОВ, шум ≤ 55 дБ(А)		по выбору заказчика до изготовления мебели	шт.	1		пом. 1; по схеме изготовителя
	Стиральная машина, место по листу ВК (ОБ_02); Ш×Г 600×600 мм	аналог по характеристикам: тип загрузки — по листу ВК, в плане 600 × 600 мм (ширина × глубина), по листу ВК		по выбору заказчика до изготовления мебели	шт.	1		пом. 13; по схеме изготовителя
	Торшер, у поз. M_17; абажур — ткань или опаловое стекло; лампа 2700 K			аналог по характеристикам	шт.	1		пом. 1; розетка P21 (ЭОМ)
	Лампа настольная, у поз. M_20; абажур — ткань или опаловое стекло; лампа 2700 K			аналог по характеристикам	шт.	1		пом. 3; розетка P9 (ЭОМ)
	Лампа настольная, у поз. M_20; абажур — ткань или опаловое стекло; лампа 2700 K			аналог по характеристикам	шт.	1		пом. 3; розетка P10 (ЭОМ)
	Торшер, у поз. M_22; абажур — ткань или опаловое стекло; лампа 2700 K			аналог по характеристикам	шт.	1		пом. 3; розетка P11 (ЭОМ)
	Торшер, у поз. M_31; абажур — ткань или опаловое стекло; лампа 2700 K			аналог по характеристикам	шт.	1		пом. 6; розетка P5 (ЭОМ)
	Лампа настольная, у поз. M_33; абажур — ткань или опаловое стекло; лампа 2700 K			аналог по характеристикам	шт.	1		пом. 7; розетка P42 (ЭОМ)
	Лампа настольная, у поз. M_43; абажур — ткань или опаловое стекло; лампа 2700 K			аналог по характеристикам	шт.	1		пом. 12; розетка P47 (ЭОМ)
	Текстиль							
T13	Портьеры-волна (гостиная); лён 70 %, вискоза 30 %; цвет NCS S 1010-Y20R; карниз 3000 мм, высота 2790 мм, сборка 2			аналог по характеристикам	шт.	2		пом. 1
T14	Тюль (гостиная); полиэстер 100 %; цвет Little Greene No. 222; карниз 3000 мм, высота 2790 мм, сборка 2,5			аналог по характеристикам	шт.	1		пом. 1
T15	Римская штора (кухня); лён 100 %; цвет Tikkurila X463; карниз 1500 мм, высота 1600 мм			аналог по характеристикам	шт.	1		пом. 1
T16	Ковёр в зоне отдыха; шерсть 100 %; цвет Tikkurila X463; 2400×2000 мм			аналог по характеристикам	шт.	1		пом. 1; с подложкой
T17	Подушки на диван; букле (шерсть 60 %, полиэстер 40 %); цвет NCS S 1010-Y20R			аналог по характеристикам	шт.	3		пом. 1
T18	Подушки на диван, акцент; хлопковый бархат 100 %; цвет NCS S 3050-R80B			аналог по характеристикам	шт.	2		пом. 1
T19	Плед на диван; альпака 50 %, шерсть 50 %; цвет Tikkurila X463			аналог по характеристикам	шт.	1		пом. 1
T7	Портьеры-волна; лён 100 %; цвет NCS S 1010-Y20R; карниз 2100 мм, высота 2890 мм, сборка 2			аналог по характеристикам	шт.	2		пом. 3
T8	Тюль; полиэстер 100 %; цвет Little Greene No. 222; карниз 2100 мм, высота 2890 мм, сборка 2,5			аналог по характеристикам	шт.	1		пом. 3
T9	Ковёр под кроватью; шерсть 100 %; цвет Tikkurila X463; 2000×1500 мм			аналог по характеристикам	шт.	1		пом. 3; с подложкой
T10	Подушки декоративные на кровать; букле (шерсть 60 %, полиэстер 40 %); цвет NCS S 1010-Y20R			аналог по характеристикам	шт.	3		пом. 3
T11	Подушки на кровать, акцент; хлопковый бархат 100 %; цвет NCS S 5020-G90Y			аналог по характеристикам	шт.	2		пом. 3
T12	Плед на кровать; шерсть мериноса 100 %; цвет NCS S 5020-G90Y			аналог по характеристикам	шт.	1		пом. 3
T1	Портьеры-волна; лён 100 %; цвет NCS S 1010-Y20R; карниз 2400 мм, высота 2890 мм, сборка 2			аналог по характеристикам	шт.	2		пом. 6
T2	Тюль; полиэстер 100 %; цвет Little Greene No. 222; карниз 2400 мм, высота 2890 мм, сборка 2,5			аналог по характеристикам	шт.	1		пом. 6
T3	Ковёр под кроватью; шерсть 80 %, хлопок 20 %; цвет Tikkurila X395; 2200×2700 мм			аналог по характеристикам	шт.	1		пом. 6; с подложкой
T4	Подушки декоративные на кровать; лён 100 %; цвет NCS S 1010-Y20R			аналог по характеристикам	шт.	3		пом. 6
T5	Подушки на кровать, акцент; хлопковый бархат 100 %; цвет Farrow & Ball No. 89			аналог по характеристикам	шт.	2		пом. 6
T6	Плед на кровать; шерсть мериноса 100 %; цвет Farrow & Ball No. 89			аналог по характеристикам	шт.	1		пом. 6
T20	Портьеры-волна; лён 100 %; цвет NCS S 1010-Y20R; карниз 2100 мм, высота 2790 мм, сборка 2			аналог по характеристикам	шт.	2		пом. 7
T21	Тюль; полиэстер 100 %; цвет Little Greene No. 222; карниз 2100 мм, высота 2790 мм, сборка 2,5			аналог по характеристикам	шт.	1		пом. 7

					Проект: Дом 120 м²		
	Лист	№ док.	Подпись	Дата	Спецификация мебели и оборудования (продолжение)	Стадия	Лист	Листов
Дизайнер	Кырлан А.С.			04.11.26		П	23	136

Поз.	Наименование и техническая характеристика	Тип, марка, обозначение документа, опросного листа	Код продукции	Поставщик	Ед. измерения	Кол.	Масса 1 ед., кг	Примечание
Т22	Ковёр под кроватью; шерсть 100 %; цвет Tikkurila X463; 1350×1900 мм			аналог по характеристикам	шт.	1		пом. 7; с подложкой
Т23	Подушки декоративные на кровать; букле (шерсть 60 %, полиэстер 40 %); цвет NCS S 1010-Y20R			аналог по характеристикам	шт.	3		пом. 7
Т24	Подушки на кровать, акцент; хлопковый бархат 100 %; цвет Farrow & Ball No. 66			аналог по характеристикам	шт.	2		пом. 7
Т25	Плед на кровать; шерсть мериноса 100 %; цвет Farrow & Ball No. 66			аналог по характеристикам	шт.	1		пом. 7
Т26	Портьеры-волна; лён 100 %; цвет NCS S 1010-Y20R; карниз 2000 мм, высота 2790 мм, сборка 2			аналог по характеристикам	шт.	2		пом. 12
Т27	Тюль; полиэстер 100 %; цвет Little Greene No. 222; карниз 2000 мм, высота 2790 мм, сборка 2,5			аналог по характеристикам	шт.	1		пом. 12
Т28	Ковёр под кроватью; шерсть 100 %; цвет Tikkurila X463; 1350×1900 мм			аналог по характеристикам	шт.	1		пом. 12; с подложкой
Т29	Подушки декоративные на кровать; букле (шерсть 60 %, полиэстер 40 %); цвет NCS S 1010-Y20R			аналог по характеристикам	шт.	3		пом. 12
Т30	Подушки на кровать, акцент; хлопковый бархат 100 %; цвет Tikkurila H440			аналог по характеристикам	шт.	2		пом. 12
Т31	Плед на кровать; шерсть мериноса 100 %; цвет Tikkurila H440			аналог по характеристикам	шт.	1		пом. 12
	Декор							
ДК6	Картина над креслом: пейзаж, масло, рама — дуб табак; 1000×800 мм; центр на 1550 мм от пола			аналог по характеристикам	шт.	1	6	пом. 1; крепление: анкер, 2 шт.
ДК7	Растение в кашпо; 450×450 мм			аналог по характеристикам	шт.	1		пом. 1
ДК8	Ваза керамическая с ветками на обеденном столе; 200×350 мм; на M_14			аналог по характеристикам	шт.	1		пом. 1
ДК40	Олива в кадке Ø450 у окна; 450×450 мм			аналог по характеристикам	шт.	1		пом. 1
ДК41	Сансевиерия в кашпо Ø400 под лестницей; 400×400 мм			аналог по характеристикам	шт.	1		пом. 2
ДК3	Картина над креслом: гравюра в паспарту, рама — графит; 550×450 мм; низ на 1050 мм от пола			аналог по характеристикам	шт.	1	4	пом. 3; крепление к стене
ДК9	Зеркало над умывальником, влагостойкое; 500×700 мм; низ на 1100 мм от пола			аналог по характеристикам	шт.	1	4	пом. 4; крепление к стене
ДК5	Зеркало; рама — чёрный матовый; 600×1800 мм; низ на 550 мм от пола			аналог по характеристикам	шт.	1	18	пом. 5; крепление: анкер, 4 шт.
ДК43	Замиокулькас в кашпо Ø350; 350×350 мм			аналог по характеристикам	шт.	1		пом. 5
ДК1	Картина над кроватью: акварель, рама — светлый дуб; 1000×700 мм; низ на 1300 мм от пола			аналог по характеристикам	шт.	1	4	пом. 6; крепление к стене
ДК44	Аглаонема в кашпо Ø400; 400×400 мм			аналог по характеристикам	шт.	1		пом. 6
ДК2	Картина над кроватью: детская иллюстрация, рама — белёный дуб; 600×450 мм; низ на 650 мм от пола			аналог по характеристикам	шт.	1	4	пом. 7; крепление к стене
ДК4	Зеркало в рост в тонкой чёрной раме; рама — чёрный матовый; 500×1600 мм; низ на 300 мм от пола			аналог по характеристикам	шт.	1	12	пом. 7; крепление: анкер для пустотелых оснований, 4 шт.
ДК45	Хлорофитум в кашпо Ø350 у окна; 350×350 мм			аналог по характеристикам	шт.	1		пом. 10
ДК46	Сансевиерия в кашпо Ø400; 400×400 мм			аналог по характеристикам	шт.	1		пом. 11
ДК10	Картина над кроватью: детский принт, рама — светлый ясень; 600×450 мм; низ на 650 мм от пола			аналог по характеристикам	шт.	1	4	пом. 12; крепление к стене
ДК11	Зеркало в рост в тонкой чёрной раме; рама — чёрный матовый; 500×1600 мм; низ на 300 мм от пола			аналог по характеристикам	шт.	1	12	пом. 12; крепление: анкер для пустотелых оснований, 4 шт.
ДК12	Зеркало над умывальником, влагостойкое; 600×750 мм; низ на 1100 мм от пола			аналог по характеристикам	шт.	1	4	пом. 13; крепление к стене

					Проект: Дом 120 м²		
	Лист	№ док.	Подпись	Дата	Спецификация мебели и оборудования (продолжение)	Стадия	Лист	Листов
Дизайнер	Кырлан А.С.			04.11.26		П	24	136

Ведомость изделий

Марка	Наименование	Пом.	Ш×Г×В, мм	Корпус	Фасад	Кромка, мм	Кол.
M_24	Шкаф-купе	5	1400×600×2650	ЛДСП 16	ЛДСП 10 мм в алюминиевом профиле	0,4 / 2	1
M_29	Шкаф распашной	6	2000×600×2600	ЛДСП 16	МДФ 18 мм, эмаль матовая	0,4 / 2	1
M_34	Шкаф распашной	7	1500×600×2200	ЛДСП 16	МДФ 18 мм, эмаль матовая	0,4 / 2	1
M_37	Система хранения	8	1600×600×2600	ЛДСП 16	без фасадов	0,4 / 2	1
M_38	Система хранения	8	800×400×2000	ЛДСП 16	без фасадов	0,4 / 2	1
M_39	Система хранения	9	2200×400×2200	ЛДСП 16	без фасадов	0,4 / 2	1
M_40	Система хранения	9	1000×400×2200	ЛДСП 16	без фасадов	0,4 / 2	1
M_44	Шкаф распашной	12	1000×600×2200	ЛДСП 16	МДФ 18 мм, эмаль матовая	0,4 / 2	1
M_46	Система хранения	12	1000×300×1200	ЛДСП 16	без фасадов	0,4 / 2	1
M_01	Модуль нижний: ящики	1	600×600×900	ЛДСП 16	МДФ 18 мм, эмаль матовая	0,4 / 2	1
M_02	Модуль нижний: мойка	1	800×600×900	ЛДСП 16	МДФ 18 мм, эмаль матовая	0,4 / 2	1
M_03	Модуль под ПММ 60: без корпуса, фасад на дверь машины	1	600×600×900	без корпуса	МДФ 18 мм, эмаль матовая — на дверь машины (навеска из её комплекта), цоколь		1
M_10	Модуль навесной: полки	1	600×350×900	ЛДСП 16	МДФ 18 мм, эмаль матовая	0,4 / 2	1
M_04	Модуль нижний: ящики	1	1040×600×900	ЛДСП 16	МДФ 18 мм, эмаль матовая	0,4 / 2	1
M_05	Модуль нижний: ящики	1	600×600×900	ЛДСП 16	МДФ 18 мм, эмаль матовая	0,4 / 2	1
M_11	Модуль навесной: полки	1	600×350×900	ЛДСП 16	МДФ 18 мм, эмаль матовая	0,4 / 2	1
M_06	Модуль нижний: духовой шкаф, варочная	1	600×600×900	ЛДСП 16	МДФ 18 мм, эмаль матовая	0,4 / 2	1
M_12	Модуль навесной: полки	1	600×350×800	ЛДСП 16	МДФ 18 мм, эмаль матовая	0,4 / 2	1
M_07	Модуль нижний: ящики	1	600×600×900	ЛДСП 16	МДФ 18 мм, эмаль матовая	0,4 / 2	1
M_13	Модуль навесной: полки	1	600×350×900	ЛДСП 16	МДФ 18 мм, эмаль матовая	0,4 / 2	1
M_08	Пенал: холодильник встр.	1	700×650×2200	ЛДСП 16	МДФ 18 мм, эмаль матовая	0,4 / 2	1
M_09	Пенал: полки	1	600×600×2200	ЛДСП 16	МДФ 18 мм, эмаль матовая	0,4 / 2	1

Ведомость встраиваемой техники

Поз.	Прибор	Ниша, вырез, мм	Вентиляция	Питание	Схема
M_02	Мойка врезная / подстольная с сифоном	вырез по шаблону, ориентир 700 × 480		смеситель — выводы ВК	по модели
M_03	Посудомоечная машина встраиваемая, 60 см	ниша 600 × 862 (от пола до низа столешницы)	зазор в цоколе, по схеме	Р32: M_04.1, H=300 — в соседнем модуле, за ящиком	по модели
M_06	Духовой шкаф встраиваемый, 60 см	ниша 560 × 600, глубина ≥ 550	зазор за шкафом, вырез в задней стенке	ЭВ2: M_07, H=150 — в соседнем модуле, за ящиком	по модели
M_06	Варочная панель индукционная, 60 см	вырез в столешнице 560 × 490		Р31: M_05, H=1175 — над столешницей (фартук)	по модели
M_08	Холодильник встраиваемый, ниша 1780	ниша 1780 × 560 × 550	решётка в цоколе, канал за корпусом, выход сверху	Р25: M_07, H=150 — в соседнем модуле, за ящиком	по модели
M_12	Вытяжка встраиваемая в навесной модуль, 60 см	низ ≥ 650 над панелью	воздуховод к вентканалу, короб до потолка	ЭВ3: M_12, H=2200 — в навесном модуле	по модели

Ведомость фурнитуры


№	Фурнитура	Тип, размер	Изделия	Кол.
1	Система дверей купе: профиль, направляющие, ролики	на 2 двери	M_24	1
2	Ручка-профиль вертикальная	в цвет профиля	M_24	2
3	Полкодержатель с фиксацией	ø5 мм	M_24, M_29, M_34, M_37, M_39, M_40, M_44, M_46, M_10, M_11, M_12, M_13, M_08, M_09	228
4	Штанга овальная 30×15, L = 676	+ 2 держателя	M_24	1
5	Полка для обуви выдвижная наклонная	ширина 676	M_24	3
6	Опора регулируемая с цоколем на клипсах	ход 20 мм	M_24, M_29, M_34, M_37, M_38, M_39, M_40, M_44	50
7	Анкер по основанию стены	по таблице крепежа	M_24, M_29, M_34, M_37, M_38, M_39, M_40, M_44, M_46, M_10, M_11, M_12, M_13	62
8	Уголок крепления к стене от опрокидывания	стальной	M_24, M_29, M_34, M_37, M_38, M_39, M_40, M_44, M_46, M_08, M_09	22
9	Петля накладная 110° с доводчиком	чашка 35 мм	M_29, M_34, M_44, M_02, M_10, M_11, M_12, M_13, M_08, M_09	86
10	Штанга овальная 30×15, L = 976	+ 2 держателя	M_29, M_34	2
11	Штанга овальная 30×15, L = 776	+ 2 держателя	M_37	1
12	Штанга выдвижная торцевая	L по глубине	M_38, M_39, M_40	5
13	Штанга овальная 30×15, L = 968	+ 2 держателя	M_44	1
14	Направляющие полного выдвижения с доводчиком NL 500	пара	M_01, M_04, M_05, M_06, M_07	16
15	Ручка-профиль	латунь матовая	M_01, M_02, M_03, M_10, M_04, M_05, M_11, M_06, M_12, M_07, M_13, M_08, M_09	32
16	Опора кухонная регулируемая 100–120 мм	+ клипса цоколя	M_01, M_02, M_04, M_05, M_06, M_07, M_08, M_09	38
17	Комплект навески фасада ПММ	из поставки машины	M_03	1
18	Навес регулируемый для навесного шкафа	пара на секцию	M_10, M_11, M_12, M_13	4
19	Шина монтажная	L = 540	M_10, M_11, M_12, M_13	4

Примечания


1. Модели техники выбирает заказчик до изготовления мебели; ниши, вырезы и вентиляция — по монтажной схеме выбранной модели (условие гарантии), её номер вносится в ведомость.
2. Количество фурнитуры — по чертежам изделий; запас крепежа 5 %. Аналоги — по характеристикам (доводчик, нагрузка, ход).
3. Цвет корпусов, фасадов и профилей — по колерной карте проекта. Кромка — скрытые / видимые торцы, мм.

					Проект: Дом 120 м²			
	Лист	№ док.	Подпись	Дата	Ведомости изделий, техники и фурнитуры	Стадия	Лист	Листов
Дизайнер	Кырлан А.С.			04.11.26		П	25	136

Фрагмент 1. Санузел гостевой (пом. 4)

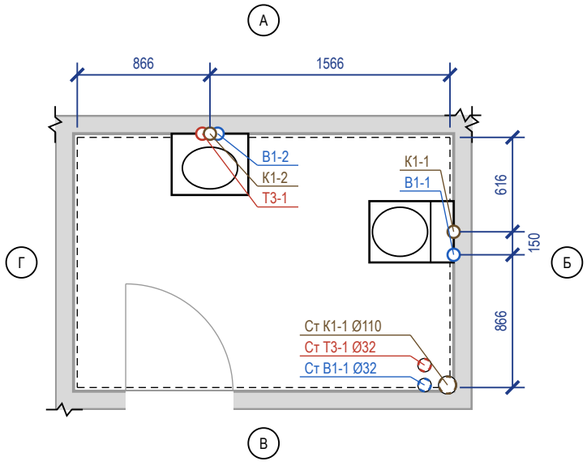

Фрагмент 2. Гостиная-кухня (пом. 1)

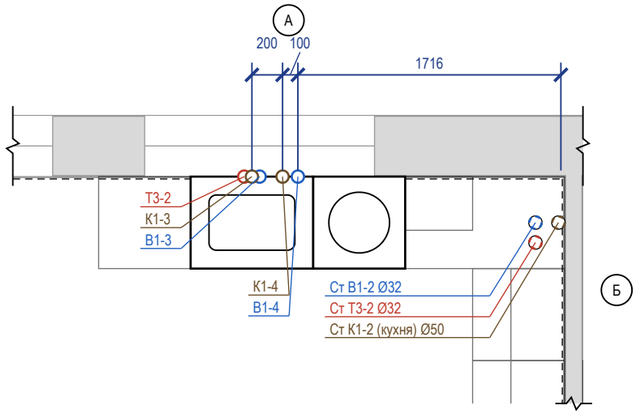

Ведомость привязок выводов

Код	Прибор	Ø	H, мм	Привязка от чист. стен, мм	Прим.
В1-1	C_01 унитаз подвесной	½"	250	ст. Б: 766 от А	в раме инсталляции
К1-1	C_01 унитаз подвесной	Ø110	220	ст. Б: 616 от А	
В1-2	C_02 умывальник	½"	600	ст. А: 916 от Г	межос. 100
Т3-1	C_02 умывальник	½"	600	ст. А: 816 от Г	межос. 100
К1-2	C_02 умывальник	Ø50	500	ст. А: 866 от Г	
В1-3	M_02 мойка кухонная	½"	600	ст. А: 1966 от Б	межос. 100
Т3-2	M_02 мойка кухонная	½"	600	ст. А: 2066 от Б	межос. 100
К1-3	M_02 мойка кухонная	Ø50	400	ст. А: 2016 от Б	
В1-4	M_03 посудомоечная машина	½"	550	ст. А: 1716 от Б	кран ПММ в шкафу мойки
К1-4	M_03 посудомоечная машина	Ø40	550	ст. А: 1816 от Б	слив ПММ в шкафу мойки

Условные обозначения


- вывод В1 (код — в ведомости привязок)
- вывод Т3 (код — в ведомости привязок)
- вывод К1 (код — в ведомости привязок)
- сантехприбор по расстановке (габарит модели)
- чистовая поверхность стены (от неё привязки)
- стояк «Ст К1-N / Ст В1-N» (ГОСТ 21.601), Ø мм
- стояк Т3 не на обмере — принят в шахте рядом со Ст В1, сверить
- линия обрыва (граница фрагмента)
- А — обозначение стены А–Г (как на развёртках)

Примечания

1. Привязки выводов даны от чистовых поверхностей стен (облицовка на сторону: санузел гостевой — 24 мм (штукатурка 10 + клей 5 + плитка 9); гостиная-кухня — 24 мм (фартук: штукатурка 10 + клей 5 + плитка 9)); эти же грани — на развёртках и в раскладке плитки. Высоты — от чистого пола помещения.
2. До черновой разводки сверить по паспорту выбранного прибора (смеситель, инсталляция, сифон).
3. Горячая вода (Т3) — слева от холодной (В1), если смотреть на прибор. Допуск установки выводов: ±5 мм в группе, ±20 мм у отдельно стоящих.
4. Расчёт систем водоснабжения и канализации и подбор оборудования выполняет проектная организация; лист задаёт места и высоты выводов.
5. Посудомоечная машина M_03: кран и слив — отдельными выводами в шкафу мойки (не за машиной), до машины ≤ 1500 мм.
6. Прибор M_02 мойка кухонная, M_03 посудомоечная машина взят из расстановки мебели (по шкафу с мойкой).
7. Ст К1-1, Ст В1-1, Ст Т3-1, Ст К1-2 (кухня), Ст В1-2, Ст Т3-2 на обмере не показаны: положение принято (исполнитель по плану заказчика), проект ВК дома не передан, не замерено; положение сверить на объекте до разметки.
8. Стояки в коробах/шахтах не замоноличивать; стояк К1 в коробе — звукоизоляция стояка в коробе без жёсткого контакта с трубой; к арматуре и ревизиям — люк не меньше 300×400.

					Проект: Дом 120 м²	М 1:40
	Лист	№ док.	Подпись	Дата		
Дизайнер	Кырлан А.С.			04.11.26	План выводов сантехники · 1-й этаж	Стадия: П; Лист: 26; Листов: 136

Фрагмент 1. Санузел второго этажа (пом. 13)

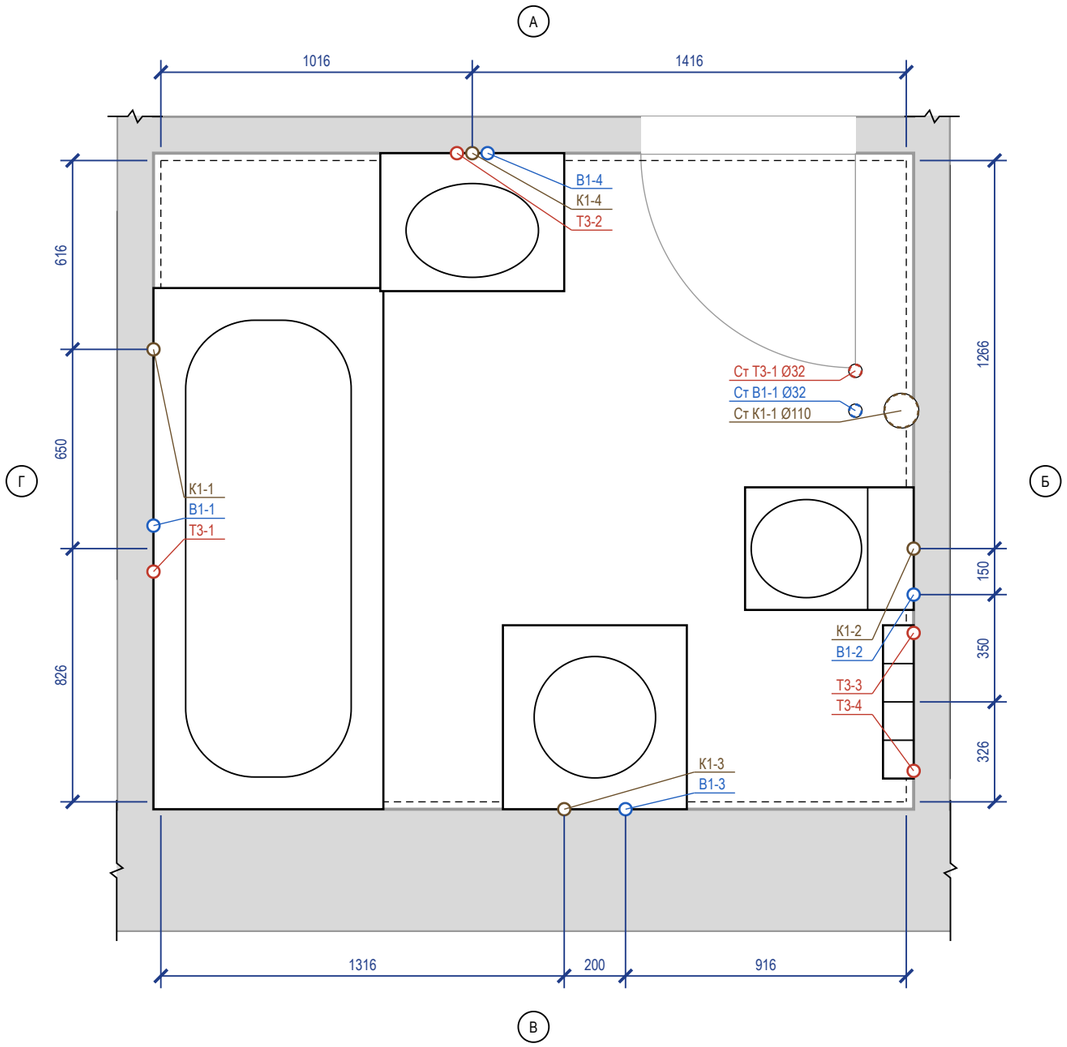

Ведомость привязок выводов

Код	Прибор	Ø	H, мм	Привязка от чист. стен, мм	Прим.
В1-1	С_03 ванна	½"	800	ст. Г: 901 от В	межос. 150
Т3-1	С_03 ванна	½"	800	ст. Г: 751 от В	межос. 150
К1-1	С_03 ванна	Ø50	50	ст. Г: 616 от А	
В1-2	С_04 унитаз подвесной	½"	250	ст. Б: 676 от В	в раме инсталляции
К1-2	С_04 унитаз подвесной	Ø110	220	ст. Б: 826 от В	
В1-3	ОБ_02 стиральная машина	½"	600	ст. В: 916 от Б	кран машины
К1-3	ОБ_02 стиральная машина	Ø50	600	ст. В: 1116 от Б	
В1-4	С_05 умывальник	½"	600	ст. А: 1066 от Г	межос. 100
Т3-2	С_05 умывальник	½"	600	ст. А: 966 от Г	межос. 100
К1-4	С_05 умывальник	Ø50	500	ст. А: 1016 от Г	
Т3-3	С_06 полотенцесушитель	½"	1150	ст. Б: 551 от В	подача, межос. 450; байпас и краны
Т3-4	С_06 полотенцесушитель	½"	1150	ст. Б: 101 от В	обратка

Условные обозначения


- вывод В1 (код — в ведомости привязок)
- вывод Т3 (код — в ведомости привязок)
- вывод К1 (код — в ведомости привязок)
- сантехприбор по расстановке (габарит модели)
- чистовая поверхность стены (от неё привязки)
- стояк «Ст К1-N / Ст В1-N» (ГОСТ 21.601), Ø мм
- стояк Т3 не на обмере — принят в шахте рядом со Ст В1, сверить
- линия обрыва (граница фрагмента)
- А — обозначение стены А–Г (как на развёртках)

Примечания


1. Привязки выводов даны от чистовых поверхностей стен (облицовка на сторону: санузел второго этажа — 24 мм (штукатурка 10 + клей 5 + плитка 9)); эти же грани — на развёртках и в раскладке плитки. Высоты — от чистого пола помещения.
2. До черновой разводки сверить по паспорту выбранного прибора (смеситель, инсталляция, сифон).
3. Горячая вода (Т3) — слева от холодной (В1), если смотреть на прибор. Допуск установки выводов: ±5 мм в группе, ±20 мм у отдельно стоящих.
4. Расчёт систем водоснабжения и канализации и подбор оборудования выполняет проектная организация; лист задаёт места и высоты выводов.
5. Ст К1-1, Ст В1-1, Ст Т3-1, Ст К1-2 (кухня), Ст В1-2, Ст Т3-2 на обмере не показаны: положение принято (исполнитель по плану заказчика), проект ВК дома не передан, не замерено; положение сверить на объекте до разметки.
6. Стояки в коробах/шахтах не замоноличивать; стояк К1 в коробе — звукоизоляция стояка в коробе без жёсткого контакта с трубой; к арматуре и ревизиям — люк не меньше 300×400.

					Проект: Дом 120 м²	М 1:20
	Лист	№ док.	Подпись	Дата		
Дизайнер	Кырлан А.С.			04.11.26	План выводов сантехники · 2-й этаж	Стадия: П; Лист: 27; Листов: 136


План этажа (М 1:200)

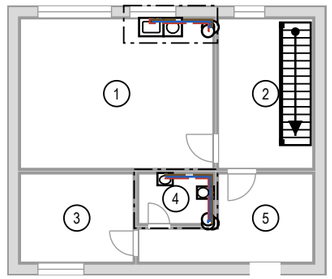

Фр. 1. Санузел гостевой (М 1:25)

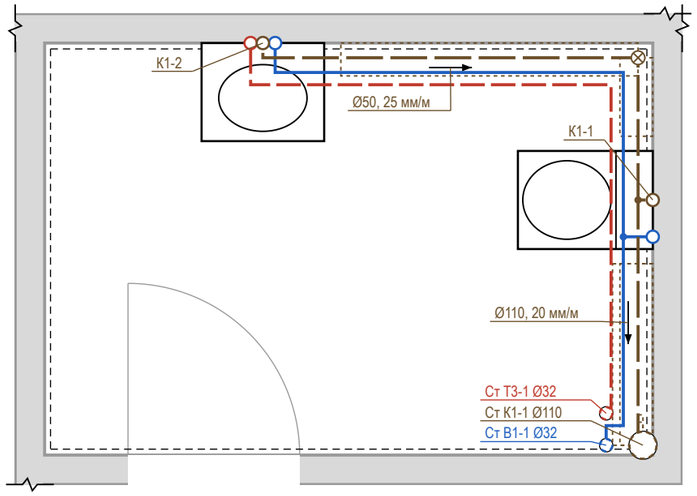

Фр. 2. Гостиная-кухня (М 1:25)

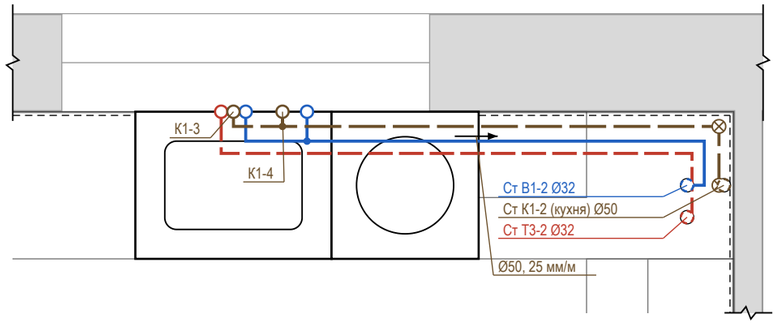

Условные обозначения


- В1 — водопровод хозяйственно-питьевой (ХВС), PP-R Ø20
- Т3 — горячее водоснабжение, подача (ГВС), PP-R Ø20
- К1 — канализация бытовая
- направление уклона К1 / пола: Ø, мм на 1 м
- ревизия (прочистка) К1 — доступ сохранить
- тройник (ответвление к прибору)
- короб К1 над чистым полом (ГКЛВ под плитку)
- вывод В1 (код — в ведомости привязок)
- вывод Т3 (код — в ведомости привязок)
- вывод К1 (код — в ведомости привязок)
- сантехприбор по расстановке (габарит модели)
- стояк «Ст К1-N / Ст В1-N» (ГОСТ 21.601), Ø мм
- стояк Т3 не на обмере — принят в шахте рядом со Ст В1, сверить
- линия обрыва (граница фрагмента)
- граница фрагмента на плане (Фр. N)

Профиль выпусков К1 (до врезки в стояк)

Выпуск	Прибор	Ø	L, м	i, мм/м	Δh, мм	Прокладка, мм
К1-1	С_01 унитаз подвесной	Ø110	1,08	20	22	короб 170×140
К1-2	С_02 умывальник	Ø50	3,19	25	80	короб 160×110
К1-3	М_02 мойка кухонная	Ø50	2,30	25	58	над полом за приборами
К1-4	М_03 посудомоечная машина	Ø40	2,10	30	63	над полом за приборами

Короб h×b: h — от чистого пола, b — от чистовой стены. Стяжка 35 мм — лист полов.

Узел ввода В1, Т3 (схема, без масштаба)

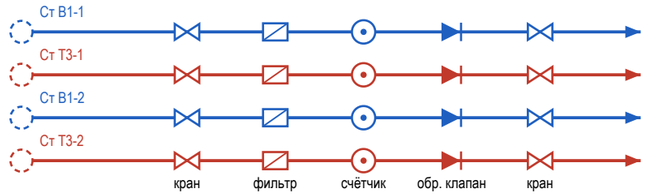

состав узла — по согласованию

⊗ Ст К1-1, Ст К1-2 (кухня): ревизия на стояке — люк в коробе

Примечания

1. Трассы принципиальные, построены от стояков вдоль стен помещений; фактическое положение фиксируется исполнительной схемой с привязками (фото с рулеткой) до закрытия.
2. Уклон К1 не менее 1/d и не более 150 мм/м (СП 30.13330.2020, п. 19.1), приняты практические уклоны; поворот — двумя отводами 45°, ревизия после поворота, доступ сохранить. Стояк К1 в коробе — звукоизоляция стояка в коробе, без жёсткого контакта короба с трубой.
3. Решение по К1: стяжка 35 мм не укрывает трубы (нужно Ø + Δh + 45 мм) — выпуски идут над чистым полом вдоль стен: К1-3, К1-4 — за приборами и в раме инсталляции; К1-1, К1-2 — в коробе ГКЛВ под плитку (размеры в профиле). Короба — на развёртках; отметку низа врезки в стояк замерить до черновых работ.
4. Состав узла ввода В1, Т3 — по согласованию: на схеме типовой узел — кран шаровой, фильтр, счётчик, обратный клапан, кран; состав и места не определены (записи реестра нет). Доступ к арматуре — через люк не меньше 300×400. Водопровод — в штробе стен или в коробах; трубы испытать давлением до закрытия (акт скрытых работ).
5. Расчёт систем, диаметры магистралей и подбор оборудования выполняет проектная организация; положение стояков, выпуск из дома и вентиляция стояков по проекту ВК дома, при его отсутствии — решение владельца с проектной организацией. Арматуру и привязки сверить по паспортам приборов.
6. Ст К1-1, Ст В1-1, Ст Т3-1, Ст К1-2 (кухня), Ст В1-2, Ст Т3-2 на обмере не показаны: положение принято (исполнитель по плану заказчика), проект ВК дома не передан, не замерено; положение сверить на объекте до разводки.


	Лист	№ док.	Подпись	Дата
Дизайнер	Кырлан А.С.			04.11.26

Проект: Дом 120 м²


Схема разводки водопровода и канализации · 1-й этаж

Стадия	Лист	Листов
П	28	136

План этажа (М 1:200)

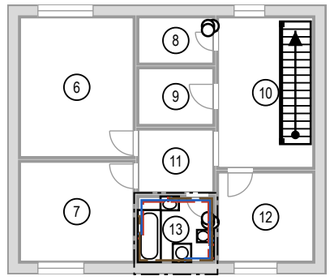

Фр. 1. Санузел второго этажа (М 1:25)

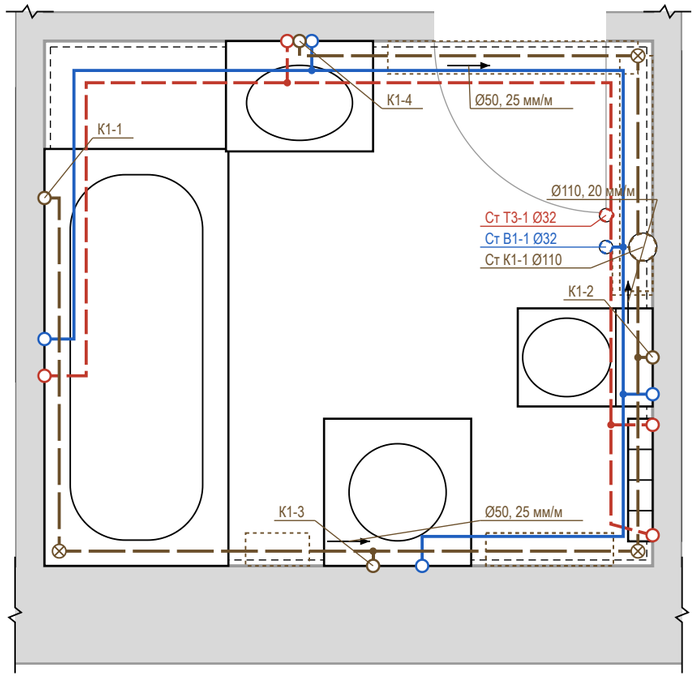

Условные обозначения


- В1 — водопровод хозяйственно-питьевой (ХВС), PP-R Ø20
- Т3 — горячее водоснабжение, подача (ГВС), PP-R Ø20
- К1 — канализация бытовая
- направление уклона К1 / пола: Ø, мм на 1 м
- ревизия (прочистка) К1 — доступ сохранить
- тройник (ответвление к прибору)
- короб К1 над чистым полом (ГКЛВ под плитку)
- вывод В1 (код — в ведомости привязок)
- вывод Т3 (код — в ведомости привязок)
- вывод К1 (код — в ведомости привязок)
- сантехприбор по расстановке (габарит модели)
- стояк «Ст К1-N / Ст В1-N» (ГОСТ 21.601), Ø мм
- стояк Т3 не на обмере — принят в шахте рядом со Ст В1, сверить
- линия обрыва (граница фрагмента)
- граница фрагмента на плане (Фр. N)

Профиль выпусков К1 (до врезки в стояк)

Выпуск	Прибор	Ø	L, м	i, мм/м	Δh, мм	Прокладка, мм
К1-2	С_04 унитаз подвесной	Ø110	0,53	20	11	короб 160×140
К1-1	С_03 ванна	Ø50	5,12	25	128	короб 210×110
К1-3	ОБ_02 стиральная машина	Ø50	2,40	25	60	короб 140×110
К1-4	С_05 умывальник	Ø50	2,24	25	56	под проёмом Д-8: короба нет; до решения

Короб h×b: h — от чистого пола, b — от чистовой стены. Стяжка 35 мм — лист полов.

Узел ввода В1, Т3 (схема, без масштаба)

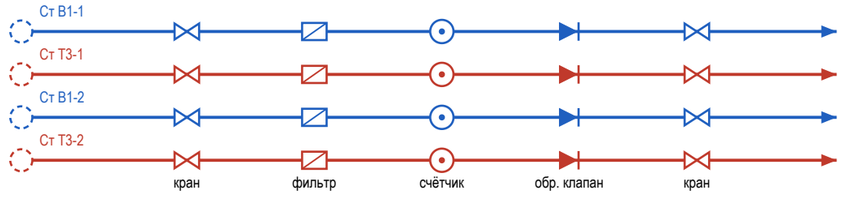

состав узла — по согласованию

- Ст К1-1, Ст К1-2 (кухня): ревизия на стояке — люк в коробе


Примечания

1. Трассы принципиальные, построены от стояков вдоль стен помещений; фактическое положение фиксируется исполнительной схемой с привязками (фото с рулеткой) до закрытия.
2. Уклон К1 не менее 1/d и не более 150 мм/м (СП 30.13330.2020, п. 19.1), приняты практические уклоны; поворот — двумя отводами 45°, ревизия после поворота, доступ сохранить. Стояк К1 в коробе — звукоизоляция стояка в коробе, без жёсткого контакта короба с трубой.
3. Решение по К1: стяжка 35 мм не укрывает трубы (нужно Ø + Δh + 45 мм) — выпуски идут над чистым полом вдоль стен; К1-2, К1-1, К1-3 — в коробе ГКЛВ под плитку (размеры в профиле). Короба — на развёртках; отметку низа врезки в стояк замерить до черновых работ.
4. К1-4 (С_05 умывальник): трасса К1 до Ст К1-1 — под проёмом Д-8, короб там не поставить: прибор ближе к стояку, выпуск в полу с подъёмом пола или насосная установка (КНС) — решение заказчика; до решения не выполнять.
5. Отводы К1-1 (5,1 м) длиннее 4 м без вентиляции — у прибора воздушный клапан Ø50 в доступном месте (за люком или в тумбе) либо вентилируемый отвод (EN 12056-2, табл. 4), подбор — проектная организация.
6. Состав узла ввода В1, Т3 — по согласованию: на схеме типовой узел — кран шаровой, фильтр, счётчик, обратный клапан, кран; состав и места не определены (записи реестра нет). Доступ к арматуре — через люк не меньше 300×400. Водопровод — в штробе стен или в коробах; трубы испытать давлением до закрытия (акт скрытых работ).
7. Расчёт систем, диаметры магистралей и подбор оборудования выполняет проектная организация; положение стояков, выпуск из дома и вентиляция стояков по проекту ВК дома, при его отсутствии — решение владельца с проектной организацией. Арматуру и привязки сверить по паспортам приборов.
8. Ст К1-1, Ст В1-1, Ст Т3-1, Ст К1-2 (кухня), Ст В1-2, Ст Т3-2 на обмере не показаны: положение принято (исполнитель по плану заказчика), проект ВК дома не передан, не замерено; положение сверить на объекте до разводки.

					Проект: Дом 120 м²
	Лист	№ док.	Подпись	Дата	Схема разводки водопровода и канализации · 2-й этаж
Дизайнер	Кырлан А.С.			04.11.26	

Стадия	Лист	Листов
П	29	136

Схема В1 (М 1:50; по вертикали и горизонтали один масштаб, глубина — ×0,5 под 45°)

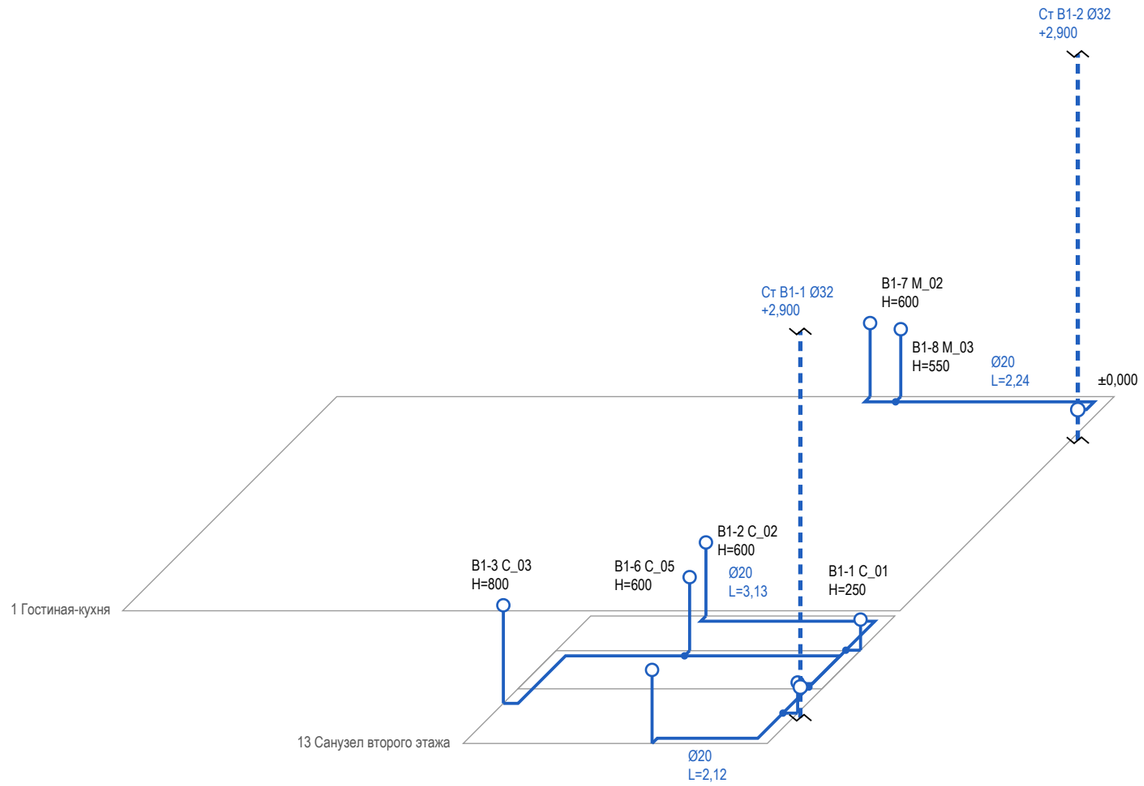

Условные обозначения


- В1 — водопровод хозяйственно-питьевой (ХВС), PP-R Ø20
- вывод В1 (код — в ведомости привязок)
- стояк «Ст К1-N / Ст В1-N» (ГОСТ 21.601), Ø мм
- стояк в плане (на отметке пола); вертикаль — стояк по высоте, разрыв — перекрытие
- тройник (ответвление к прибору)
- кран шаровой
- стояк Т3 не на обмере — принят в шахте рядом со Ст В1, сверить

Примечания

1. Схема В1 построена по тем же трассам, что план разводки: положение в плане сохранено, глубина — в масштабе ×0,5. Трассы принципиальные; фактическое положение фиксируется исполнительной схемой до закрытия.
2. Высоты Н — от чистого пола помещения, мм. Отметка прокладки магистрали В1 (в стяжке, в стене или по полу) в данных не задана: участки показаны на уровне пола условно (записи реестра нет).
3. Узел ввода В1 (кран, фильтр, счётчик, обратный клапан, кран) — на схеме разводки; состав узла ввода — по согласованию. Кран шаровой — на первом участке от стояка.
4. Ст В1-1, Ст В1-2 на обмере не показаны: положение принято (исполнитель по плану заказчика), проект ВК дома не передан, не замерено; положение сверить на объекте до разводки.
5. Трубы испытать давлением до закрытия (акт скрытых работ, опрессовка по СП 73.13330.2016).
6. Диаметры, высоты выводов и места кранов — по паспортам выбранных приборов и расчёту проектной организации.
7. Расчёт систем, диаметры магистралей и подбор оборудования выполняет проектная организация.

					Проект: Дом 120 м²		**М 1:50**
	Лист	№ док.	Подпись	Дата	Аксонометрическая схема В1 (холодное водоснабжение)	Стадия	Лист	Листов
Дизайнер	Кырлан А.С.			04.11.26		П	30	136

Схема Т3 (М 1:50; по вертикали и горизонтали один масштаб, глубина — ×0,5 под 45°)

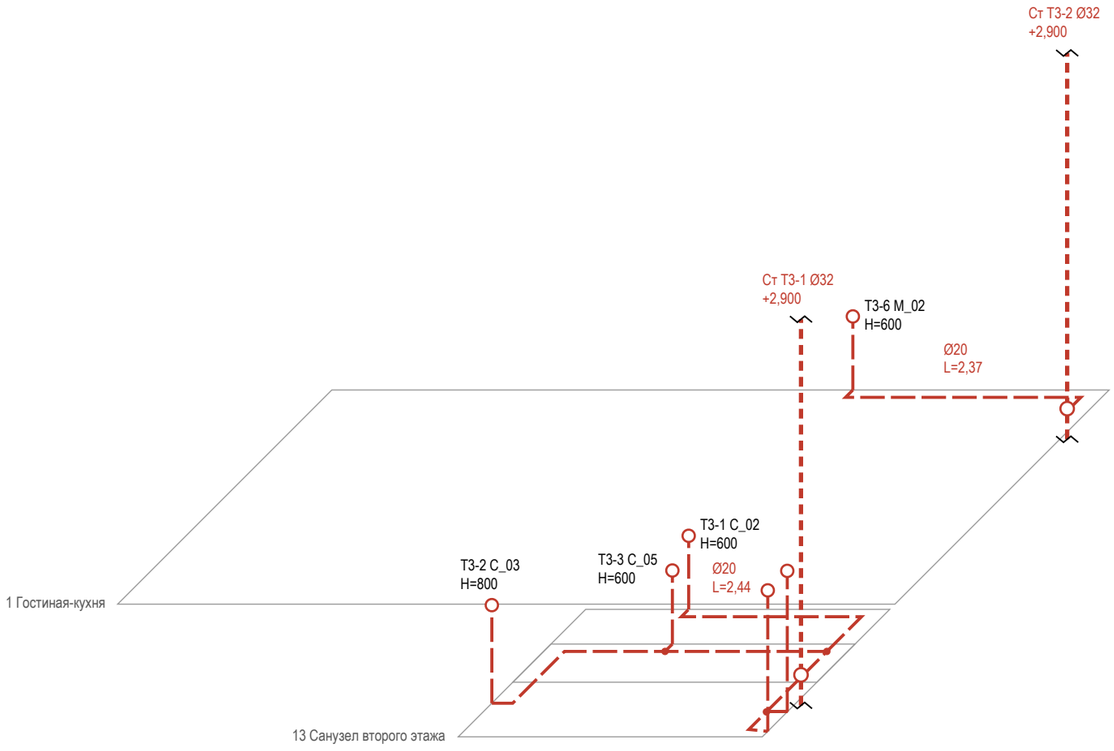

Условные обозначения


- Т3 — горячее водоснабжение, подача (ГВС), PP-R Ø20
- вывод Т3 (код — в ведомости привязок)
- стояк «Ст К1-N / Ст В1-N» (ГОСТ 21.601), Ø мм
- стояк в плане (на отметке пола); вертикаль — стояк по высоте, разрыв — перекрытие
- тройник (ответвление к прибору)
- кран шаровой
- стояк Т3 не на обмере — принят в шахте рядом со Ст В1, сверить

Примечания

1. Схема Т3 построена по тем же трассам, что план разводки: положение в плане сохранено, глубина — в масштабе ×0,5. Трассы принципиальные; фактическое положение фиксируется исполнительной схемой до закрытия.
2. Высоты Н — от чистого пола помещения, мм. Отметка прокладки магистрали Т3 (в стяжке, в стене или по полу) в данных не задана: участки показаны на уровне пола условно (записи реестра нет).
3. Узел ввода Т3 (кран, фильтр, счётчик, обратный клапан, кран) — на схеме разводки; состав узла ввода — по согласованию. Кран шаровой — на первом участке от стояка.
4. Циркуляция ГВС в данных не задана — циркуляционного трубопровода на схеме нет (записи реестра нет).
5. Ст Т3-1, Ст Т3-2 на обмере не показаны: положение принято (исполнитель по плану заказчика), проект ВК дома не передан, не замерено; положение сверить на объекте до разводки.
6. Трубы испытать давлением до закрытия (акт скрытых работ, опрессовка по СП 73.13330.2016).
7. Диаметры, высоты выводов и места кранов — по паспортам выбранных приборов и расчёту проектной организации.
8. Расчёт систем, диаметры магистралей и подбор оборудования выполняет проектная организация.

					Проект: Дом 120 м²	М 1:50
	Лист	№ док.	Подпись	Дата	Аксонометрическая схема Т3 (горячее водоснабжение)	Стадия / Лист / Листов
Дизайнер	Кырлан А.С.			04.11.26		П / 31 / 136

Схема К1 (М 1:50; по вертикали и горизонтали один масштаб, глубина — ×0,5 под 45°)

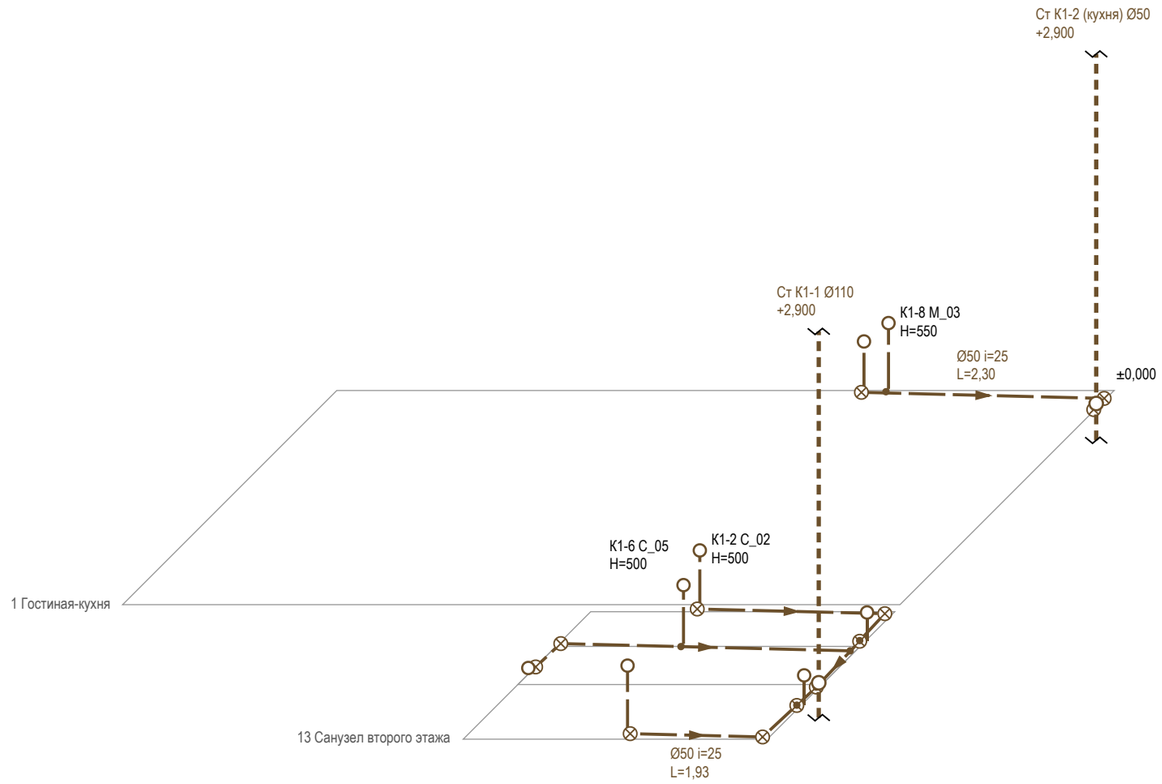

Условные обозначения


- К1 — канализация бытовая
- вывод К1 (код — в ведомости привязок)
- стояк «Ст К1-N / Ст В1-N» (ГОСТ 21.601), Ø мм
- стояк в плане (на отметке пола); вертикаль — стояк по высоте, разрыв — перекрытие
- направление уклона К1 / пола: Ø, мм на 1 м
- ревизия (прочистка) К1 — доступ сохранить
- тройник (ответвление к прибору)
- стояк Т3 не на обмере — принят в шахте рядом со Ст В1, сверить

Примечания

1. Схема К1 построена по тем же трассам, что план разводки: положение в плане сохранено, глубина — в масштабе ×0,5. Трассы принципиальные; фактическое положение фиксируется исполнительной схемой до закрытия.
2. Отметки — от плиты перекрытия: низ трубы у врезки в стояк — отметка из данных выпуска, к прибору труба поднимается на уклон i, мм/м (уклон не менее 1/d и не более 150 мм/м, СП 30.13330.2020, п. 19.1); чистый пол — выше плиты на стяжку (высота пирога пола). Высота выпуска прибора H — от чистого пола.
3. Ревизия — на повороте и в начале участка; стояк К1 в коробе с люком — звукоизоляция стояка в коробе; поворот — двумя отводами 45°.
4. Ст К1-1, Ст К1-2 (кухня) на обмере не показаны: положение принято (исполнитель по плану заказчика), проект ВК дома не передан, не замерено; положение сверить на объекте до разводки.
5. Трубы испытать давлением до закрытия (акт скрытых работ, опрессовка по СП 73.13330.2016).
6. Диаметры, высоты выводов и места кранов — по паспортам выбранных приборов и расчёту проектной организации.
7. Расчёт систем, диаметры магистралей и подбор оборудования выполняет проектная организация.

					Проект: Дом 120 м² — **М 1:50**
	Лист	№ док.	Подпись	Дата	Аксонометрическая схема К1 (канализация)
Дизайнер	Кырлан А.С.			04.11.26	Стадия: П; Лист: 32; Листов: 136

Стена А (М 1:20)

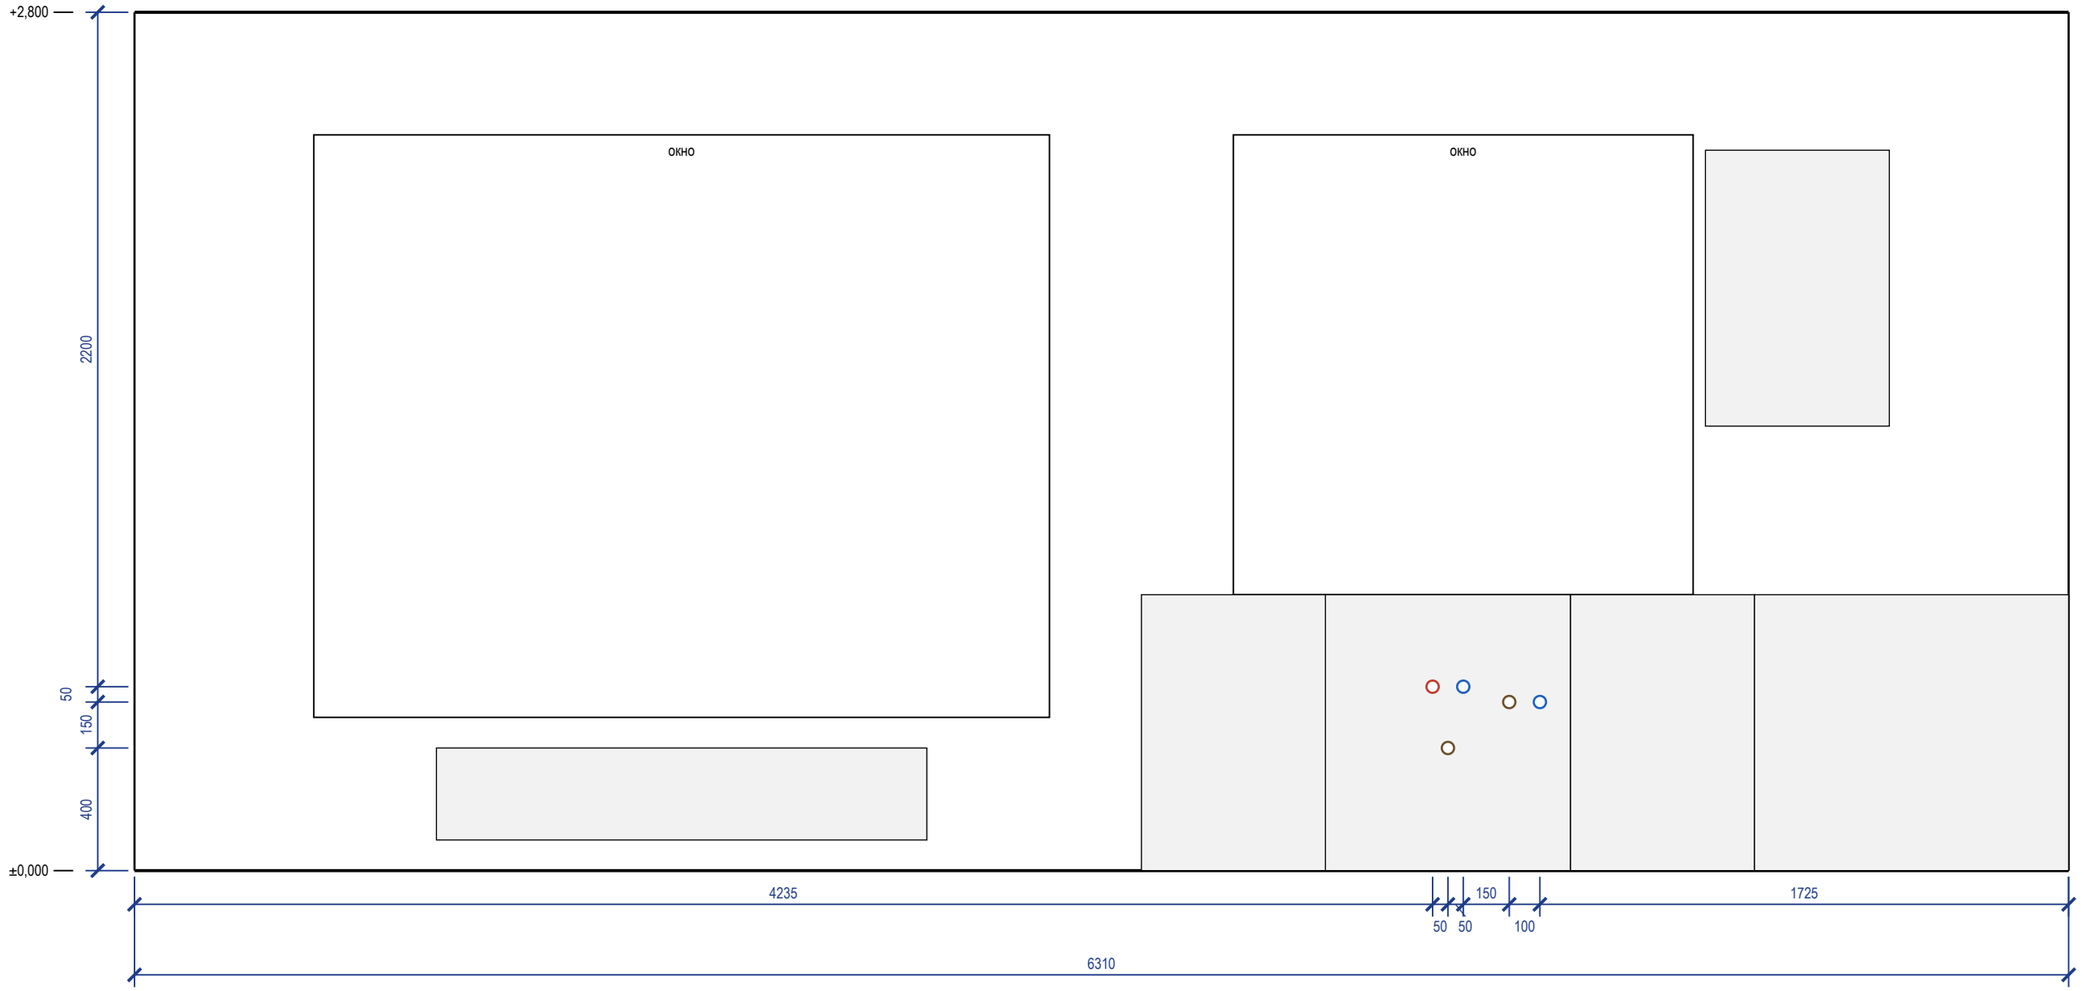

Ведомость привязок выводов (от чистого пола и угла)

Код	Прибор	Ø	H, мм	Привязка, мм
В1-7	М_02 мойка кухонная	½"	600	ст. А: 4335 от лев. угла
Т3-6	М_02 мойка кухонная	½"	600	ст. А: 4235 от лев. угла
К1-7	М_02 мойка кухонная	Ø50	400	ст. А: 4285 от лев. угла
В1-8	М_03 посудомоечная машина	½"	550	ст. А: 4585 от лев. угла
К1-8	М_03 посудомоечная машина	Ø40	550	ст. А: 4485 от лев. угла

Условные обозначения

- вывод В1 (код — в ведомости привязок)
- вывод Т3 (код — в ведомости привязок)
- вывод К1 (код — в ведомости привязок)
- сантехприбор по расстановке (габарит модели)
- дверной проём; окно — сплошной контур


Примечания

1. Габариты и высоты приборов, межосевые смесителей и места кранов — по паспортам выбранных приборов, сверяются до разметки стен.
2. Высоты H — от чистого пола помещения, мм; отметка чистого пола и потолка — у левого края вида (от ±0,000 объекта). Привязки — от левого чистового угла вида (облицовка стен вычтена), как на развёртках стен.
3. Стояки в помещении: Ст К1-2 (кухня) Ø50, Ст В1-2 Ø32, Ст Т3-2 Ø32 — положение на плане выводов; выводы подключаются к ним по схеме разводки.
4. Ревизионные люки к арматуре и ревизиям в данных не заданы: место и размер не определены (записи реестра нет).
5. Мойка, ПММ и фильтр — выводы в шкафу мойки; диаметры и положение сифона и кранов сверить по паспортам приборов и чертежам модуля.
6. Часть подписей выводов не уместилась у знака: коды и высоты — в ведомости привязок.
7. Расчёт систем водоснабжения и канализации и подбор оборудования выполняет проектная организация; лист задаёт места и высоты выводов.


					Проект: Дом 120 м²	М 1:20
	Лист	№ док.	Подпись	Дата		
Дизайнер	Кырлан А.С.			04.11.26	Развёртки мокрых зон: выводы ВК. Гостиная-кухня	Стадия: П; Лист: 33; Листов: 136

выпуск 04.11.2026 № 406ed8a6ce · стр. 33 из 136

Стена А (М 1:20)

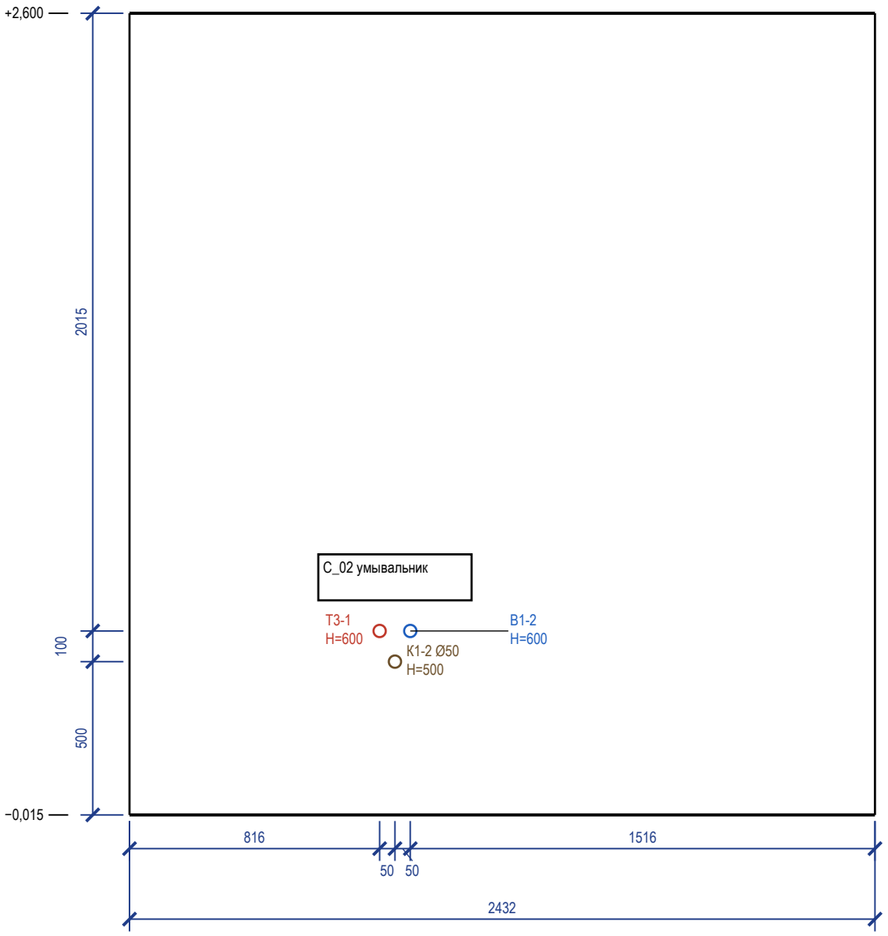

Стена Б (М 1:20)

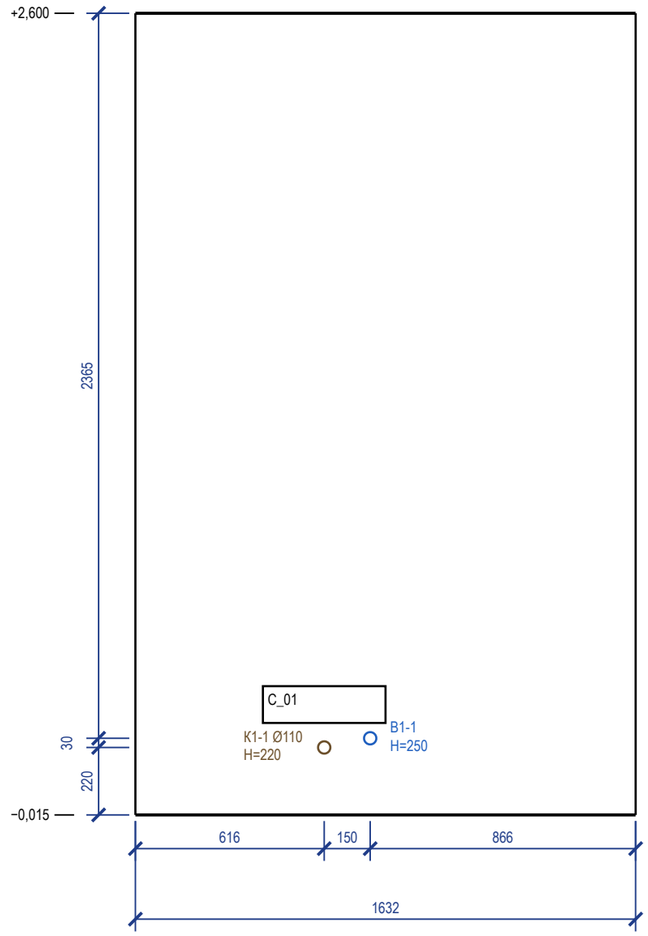

Ведомость привязок выводов (от чистого пола и угла)

Код	Прибор	Ø	H, мм	Привязка, мм
B1-2	C_02 умывальник	½"	600	ст. А: 916 от лев. угла
T3-1	C_02 умывальник	½"	600	ст. А: 816 от лев. угла
K1-2	C_02 умывальник	Ø50	500	ст. А: 866 от лев. угла
B1-1	C_01 унитаз подвесной	½"	250	ст. Б: 766 от лев. угла
K1-1	C_01 унитаз подвесной	Ø110	220	ст. Б: 616 от лев. угла

Условные обозначения


- вывод B1 (код — в ведомости привязок)
- вывод T3 (код — в ведомости привязок)
- вывод K1 (код — в ведомости привязок)
- сантехприбор по расстановке (габарит модели)
- дверной проём; окно — сплошной контур

Примечания


1. Габариты и высоты приборов, межосевые смесителей и места кранов — по паспортам выбранных приборов, сверяются до разметки стен.
2. Высоты H — от чистого пола помещения, мм; отметка чистого пола и потолка — у левого края вида (от ±0,000 объекта). Привязки — от левого чистового угла вида (облицовка стен вычтена), как на развёртках стен.
3. Стояки в помещении: Ст K1-1 Ø110, Ст B1-1 Ø32, Ст T3-1 Ø32 — положение на плане выводов; выводы подключаются к ним по схеме разводки.
4. Ревизионные люки к арматуре и ревизиям в данных не заданы: место и размер не определены (записи реестра нет).
5. Расчёт систем водоснабжения и канализации и подбор оборудования выполняет проектная организация; лист задаёт места и высоты выводов.

					Проект: Дом 120 м²	М 1:20
	Лист	№ док.	Подпись	Дата		
Дизайнер	Кырлан А.С.			04.11.26	Развёртки мокрых зон: выводы ВК. Санузел гостевой	Стадия: П; Лист: 34; Листов: 136

Стена А (М 1:20)

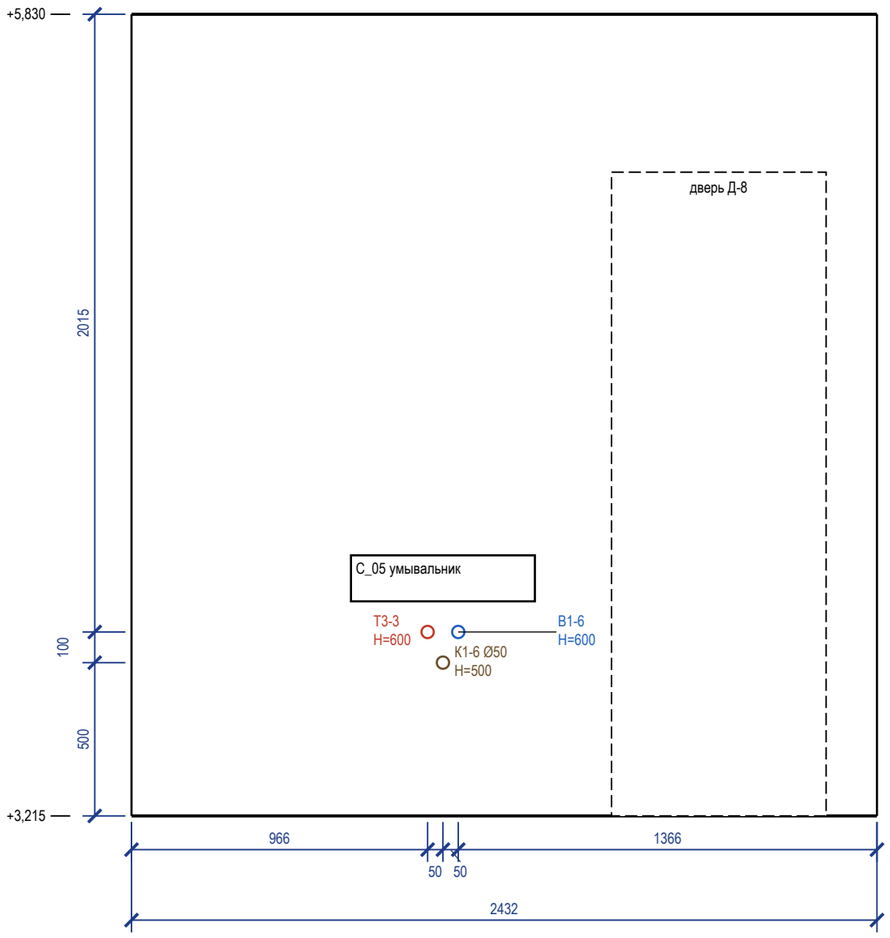

Стена Б (М 1:20)

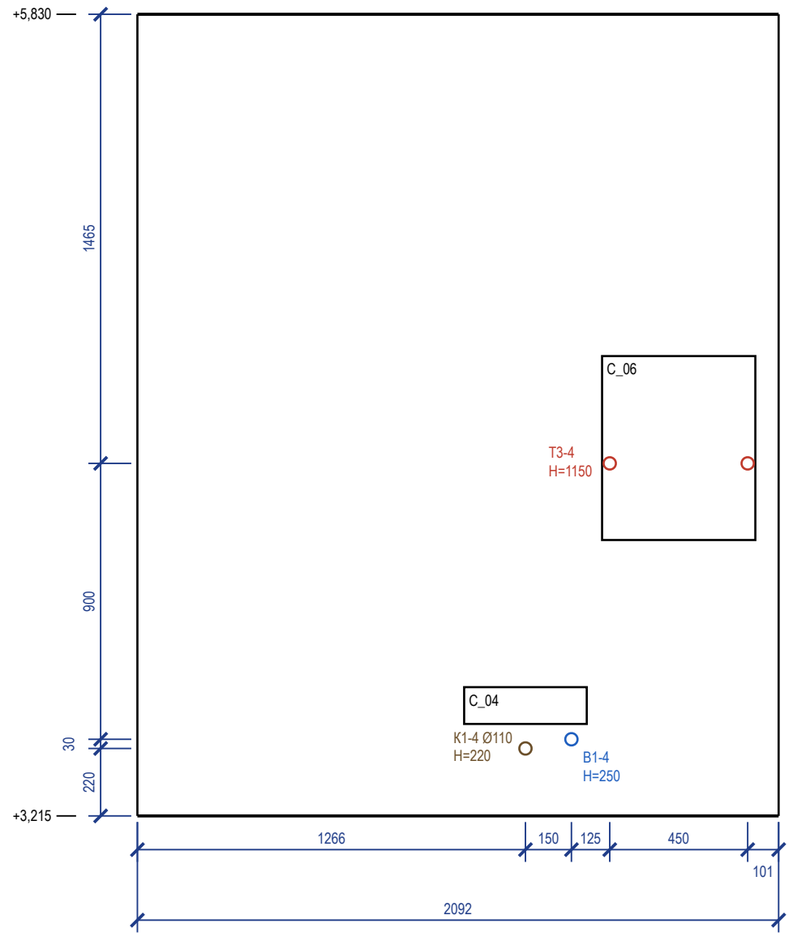

Ведомость привязок выводов (от чистого пола и угла)

Код	Прибор	Ø	H, мм	Привязка, мм
B1-6	C_05 умывальник	½"	600	ст. А: 1066 от лев. угла
T3-3	C_05 умывальник	½"	600	ст. А: 966 от лев. угла
K1-6	C_05 умывальник	Ø50	500	ст. А: 1016 от лев. угла
B1-4	C_04 унитаз подвесной	½"	250	ст. Б: 1416 от лев. угла
K1-4	C_04 унитаз подвесной	Ø110	220	ст. Б: 1266 от лев. угла
T3-4	C_06 полотенцесушитель	½"	1150	ст. Б: 1541 от лев. угла
T3-5	C_06 полотенцесушитель	½"	1150	ст. Б: 1991 от лев. угла

Условные обозначения

- вывод B1 (код — в ведомости привязок)
- вывод T3 (код — в ведомости привязок)
- вывод K1 (код — в ведомости привязок)
- сантехприбор по расстановке (габарит модели)
- дверной проём; окно — сплошной контур


Примечания

1. Габариты и высоты приборов, межосевые смесителей и места кранов — по паспортам выбранных приборов, сверяются до разметки стен.
2. Высоты H — от чистого пола помещения, мм; отметка чистого пола и потолка — у левого края вида (от ±0,000 объекта). Привязки — от левого чистового угла вида (облицовка стен вычтена), как на развёртках стен.
3. Ревизионные люки к арматуре и ревизиям в данных не заданы: место и размер не определены (записи реестра нет).
4. Часть подписей выводов не уместилась у знака: коды и высоты — в ведомости привязок.
5. Помещение «Санузел второго этажа» — 2 листа: стены 1) А, Б; 2) В, Г.
6. Расчёт систем водоснабжения и канализации и подбор оборудования выполняет проектная организация; лист задаёт места и высоты выводов.


					Проект: Дом 120 м²	М 1:20
	Лист	№ док.	Подпись	Дата	Развёртки мокрых зон: выводы ВК. Санузел второго этажа (лист 1 из 2)	
Дизайнер	Кырлан А.С.			04.11.26		

Стадия	Лист	Листов
П	35	136

Стена В (М 1:20)

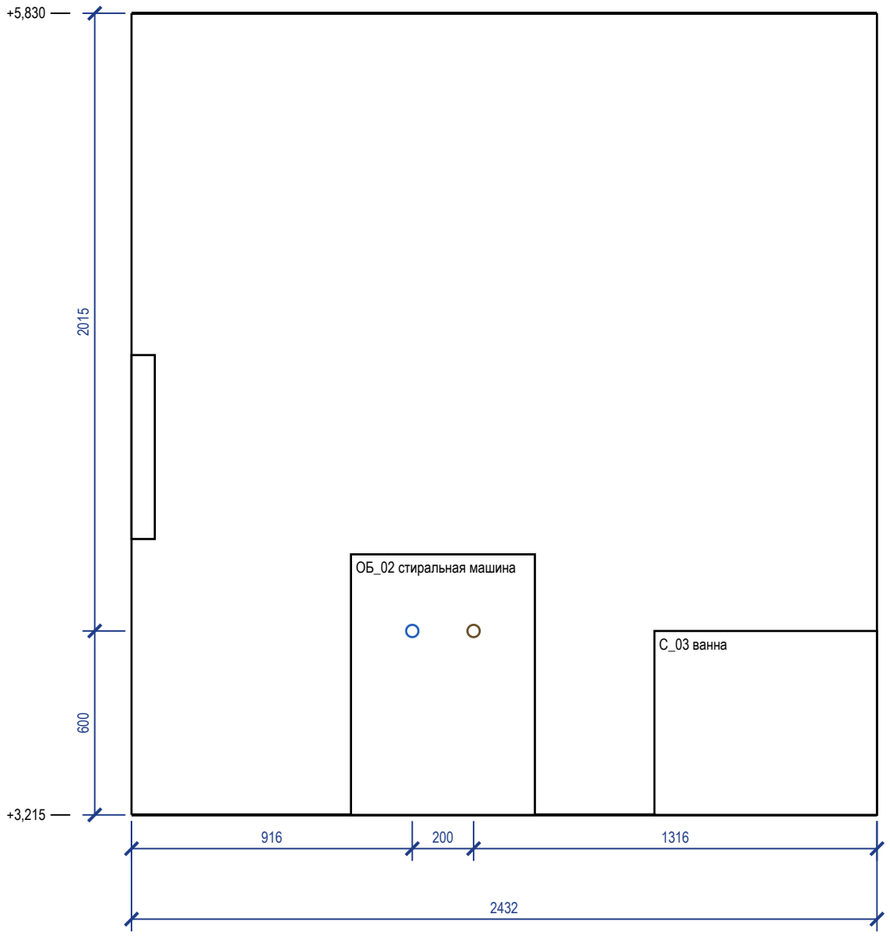

Стена Г (М 1:20)

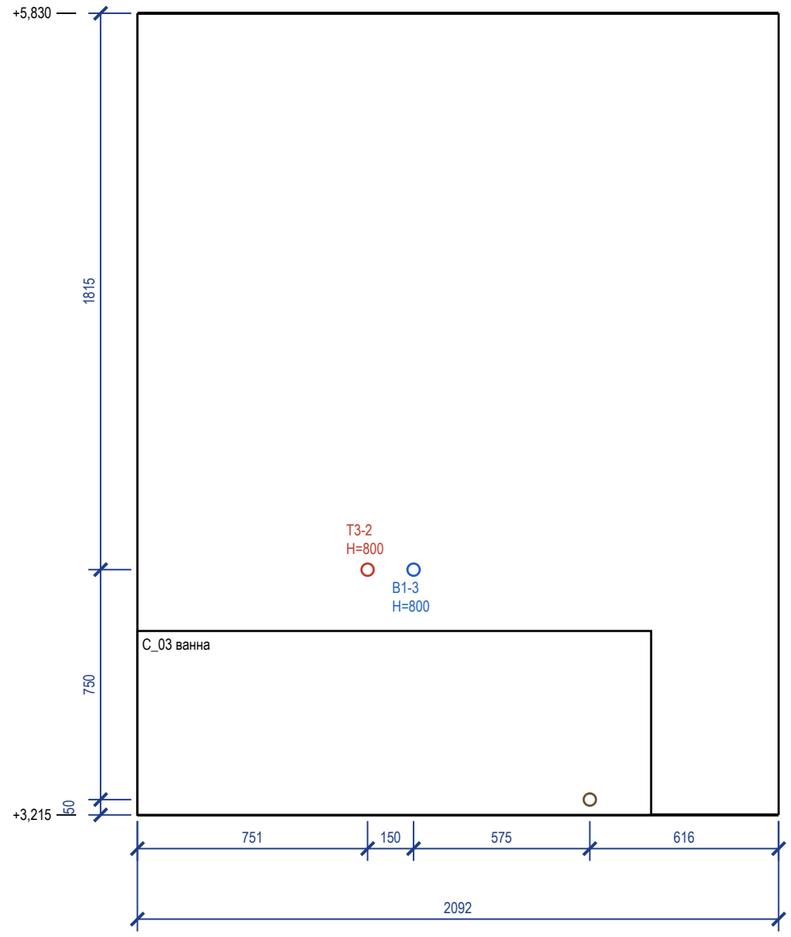

Ведомость привязок выводов (от чистого пола и угла)

Код	Прибор	Ø	H, мм	Привязка, мм
В1-5	ОБ_02 стиральная машина	½"	600	ст. В: 916 от лев. угла
К1-5	ОБ_02 стиральная машина	Ø50	600	ст. В: 1116 от лев. угла
В1-3	С_03 ванна	½"	800	ст. Г: 901 от лев. угла
Т3-2	С_03 ванна	½"	800	ст. Г: 751 от лев. угла
К1-3	С_03 ванна	Ø50	50	ст. Г: 1476 от лев. угла

Условные обозначения

- вывод В1 (код — в ведомости привязок)
- вывод Т3 (код — в ведомости привязок)
- вывод К1 (код — в ведомости привязок)
- сантехприбор по расстановке (габарит модели)
- дверной проём; окно — сплошной контур

Примечания

1. Габариты и высоты приборов, межосевые смесителей и места кранов — по паспортам выбранных приборов, сверяются до разметки стен.
2. Высоты H — от чистого пола помещения, мм; отметка чистого пола и потолка — у левого края вида (от ±0,000 объекта). Привязки — от левого чистового угла вида (облицовка стен вычтена), как на развёртках стен.
3. Ревизионные люки к арматуре и ревизиям в данных не заданы: место и размер не определены (записи реестра нет).
4. Часть подписей выводов не уместилась у знака: коды и высоты — в ведомости привязок.
5. Помещение «Санузел второго этажа» — 2 листа: стены 1) А, Б; 2) В, Г.
6. Расчёт систем водоснабжения и канализации и подбор оборудования выполняет проектная организация; лист задаёт места и высоты выводов.

					Проект: Дом 120 м²	М 1:20
	Лист	№ док.	Подпись	Дата	Развёртки мокрых зон: выводы ВК. Санузел второго этажа (лист 2 из 2)	
Дизайнер	Кырлан А.С.			04.11.26		


Стадия	Лист	Листов
П	36	136

Поз.	Наименование и техническая характеристика	Тип, марка, обозначение документа	Код продукции	Поставщик	Ед. изм.	Кол.	Масса 1 ед., кг	Примечание
	Санитарные приборы							
1	Ванна встраиваемая акриловая 1700×750 мм, с каркасом, экраном и отверстием слив-перелив	аналог		выбор заказчика	шт	1		С_03
2	Унитаз подвесной безободковый, с сиденьем микролифт, крепёж и звукоизолирующая прокладка	Jacob Delafon Struktura EDF102-00		выбор заказчика	шт	2		С_01, С_04
3	Инсталляция для подвесного унитаза: рама высотой 1120 мм, бачок, клавиша смыва (ось клавиши 1050 мм от чистого пола)	аналог		выбор заказчика	шт	2		С_01, С_04; короб ГКЛВ
4	Умывальник подвесной 500×400 мм, с отверстием под смеситель и переливом	аналог		выбор заказчика	шт	1		С_02
5	Умывальник подвесной 600×450 мм, с отверстием под смеситель и переливом	аналог		выбор заказчика	шт	1		С_05
6	Мойка кухонная врезная / подстольная, с переливом, ориентир 700×480 мм — в модуле М_02 шириной 800 мм, вырез по шаблону модели	аналог		с кухонной мебелью	шт	1		М_02
7	Полотенцесушитель водяной (ГВС), с байпасом и кранами	аналог		выбор заказчика	шт	1		С_06
	Смесители, сифоны и арматура приборов							
8	Смеситель для ванны настенный однорычажный, межосевое 150 мм, с душевым набором (лейка, шланг, держатель)	аналог		выбор заказчика	шт	1		С_03
9	Смеситель для умывальника однорычажный, с донным клапаном	аналог		выбор заказчика	шт	2		С_02, С_05
10	Смеситель кухонный однорычажный, высокий излив	аналог		выбор заказчика	шт	1		М_02
11	Обвязка ванны слив-перелив Ø40/50 с сифоном	аналог		выбор заказчика	шт	1		С_03
12	Сифон для умывальника бутылочный Ø32/40–50, с гофрой к выпуску	аналог		выбор заказчика	шт	2		С_02, С_05
13	Сифон для мойки Ø40/50	аналог		выбор заказчика	шт	1		М_02
14	Сифон для посудомоечной машины с обратным клапаном, на выводе слива Ø40	аналог		выбор заказчика	шт	1		М_03
15	Сифон для стиральной машины встраиваемый в стену Ø50, с обратным клапаном	аналог		выбор заказчика	шт	1		ОБ_02
16	Кран угловой ½"×½" с гибкой подводкой 40 см (умывальники, мойка)	аналог		выбор заказчика	шт	6		по 2 на прибор
17	Кран шаровой угловой ½"×¾" для подключения стиральной и посудомоечной машины	аналог		выбор заказчика	шт	2		ОБ_02, М_03
18	Узел подключения полотенцесушителя: байпас Ду20, краны шаровые ½" ×2	аналог		выбор заказчика	шт	1		
	Трубопроводы							
19	Труба полипропиленовая PP-R PN20 Ø20×3,4 (В1)	ГОСТ 32415-2013		выбор заказчика	м	18,5	0,17	12,2 + 4,3 + 10 %
20	Труба PP-R, армированная стекловолокном, PN20 Ø20×2,8 (Т3)	ГОСТ 32415-2013		выбор заказчика	м	17,5	0,15	10,7 + 4,9 + 10 %
21	Труба канализационная ПП Ø40 (К1)	ГОСТ 32414-2013		выбор заказчика	м	1		0,1 + 0,6 + 10 %
22	Труба канализационная ПП Ø50 (К1)	ГОСТ 32414-2013		выбор заказчика	м	13		9,5 + 2,0 + 10 %
23	Труба канализационная ПП Ø110 (К1)	ГОСТ 32414-2013		выбор заказчика	м	2,5		1,6 + 0,4 + 10 %
	Фасонные части и выводы							
24	Отвод канализационный ПП 45° Ø50	ГОСТ 32414-2013		выбор заказчика	шт	18		2 шт. на поворот
25	Отвод канализационный ПП 45° Ø110	ГОСТ 32414-2013		выбор заказчика	шт	6		2 шт. на поворот
26	Тройник канализационный ПП 45° (врезки ветвей)	ГОСТ 32414-2013		выбор заказчика	шт	7		
27	Ревизия канализационная ПП (после поворота трассы)	ГОСТ 32414-2013		выбор заказчика	шт	6		доступ сохранить
28	Фитинги PP-R Ø20: тройники, угольники 90° (ветви и повороты В1, Т3)	ГОСТ 32415-2013		выбор заказчика	шт	35		
29	Водорозетка PP-R Ø20×½" настенная, с креплением	ГОСТ 32415-2013		выбор заказчика	шт	14		коды — лист выводов
30	Кран шаровой латунный Ду15 PN16 (отключение ввода)	аналог		выбор заказчика	шт	4		Ст В1-1, Ст Т3-1, Ст В1-2, Ст Т3-2
31	Фильтр сетчатый косой Ду15	аналог		выбор заказчика	шт	4		
32	Счётчик воды крыльчатый Ду15 (ХВ, ГВ), с поверкой	аналог		выбор заказчика	шт	4		пломба УК
33	Клапан обратный Ду15	аналог		выбор заказчика	шт	4		
34	Люк ревизионный нажимной под плитку 300×400 мм	аналог		выбор заказчика	шт	2		к стоякам и арматуре
35	Звукоизоляция стояка К1 в коробе: рулонный звукоизоляционный материал ≥ 10 мм, обмотка стояка на высоту этажа	аналог		выбор заказчика	м	5,8		Ст К1-1, Ст К1-2 (кухня)
36	Короб К1 над полом: профиль ПН/ПС, ГКЛВ 12,5 мм под плитку	аналог		выбор заказчика	м	9,5		сечение — лист разводки

Примечания

1. Форма 1 ГОСТ 21.110-2013, ширины граф изменены по п. 4.1. «Аналог» — аналог по характеристикам: модели внести до черновых работ, привязки выводов сверить по паспортам.
2. Бытовая техника не входит (показана арматура подключения), мойка — в комплекте кухни (марка — модуля кухни, как у столяра). Длины труб — трасса листа разводки + подъёмы + 10 %.
3. Стояк К1 в коробе — звукоизоляция стояка в коробе без жёсткого контакта короба с трубой.
4. Расчёт систем водоснабжения и канализации, диаметры магистралей и подбор оборудования выполняет проектная организация.

					Проект: Дом 120 м²		
	Лист	№ док.	Подпись	Дата	Спецификация сантехнического оборудования	Стадия	Лист	Листов
Дизайнер	Кырлан А.С.			04.11.26		П	37	136

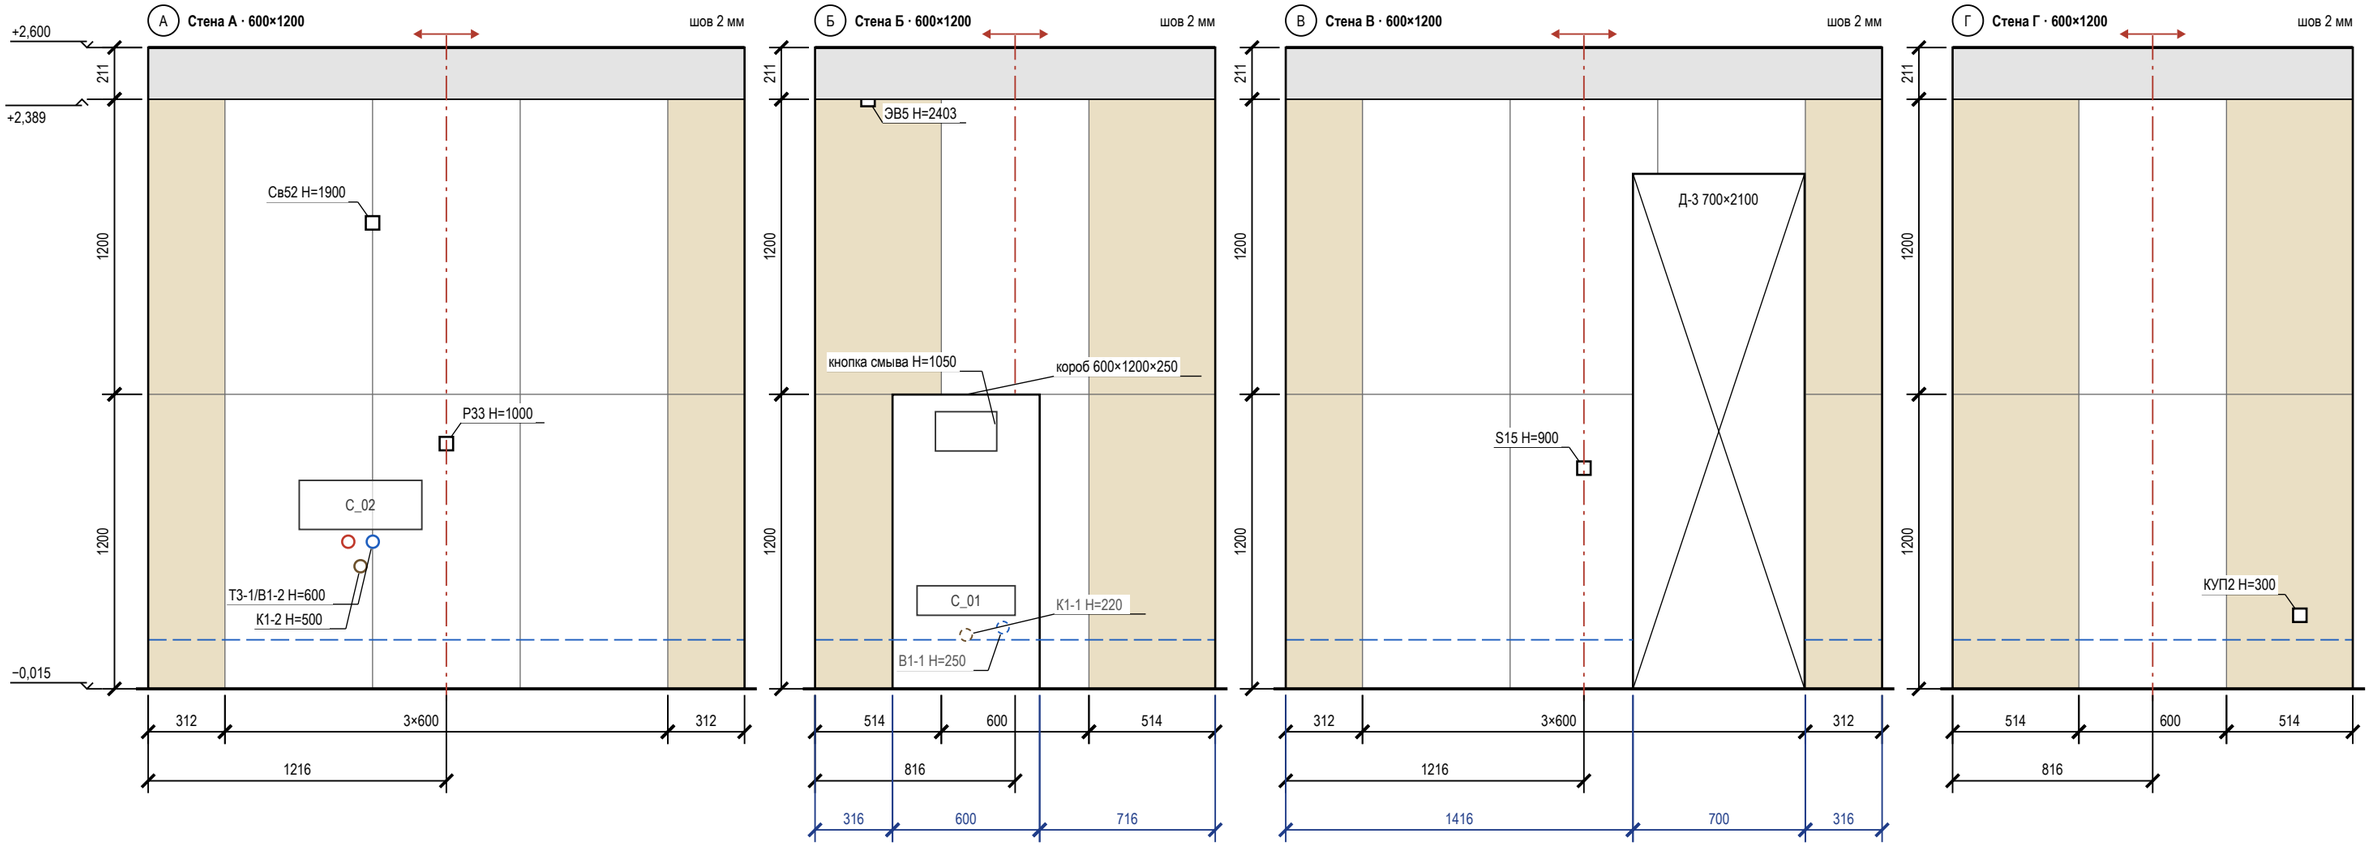

Подсчёт плитки по стенам и коробу

Поверхность	L × H, мм	S, м²	Целых	Подр.	С запасом	Подрезки: край / верх, мм
стена А	2432 × 2404	5,96	6	4	11	312 / 312; целый ряд
стена Б	1632 × 2404	3,32	1	5	7	514 / 514; целый ряд
короб (ст. Б)	600×1200×250	1,47	1	3	5	лицо 600; бок. 250
стена В	2432 × 2404	4,49	2	8	11	312 / 312; целый ряд
стена Г	1632 × 2404	2,90	2	4	7	514 / 514; целый ряд
Итого		**18,15**	**12**	**24**	**41**	

Условные обозначения

- плитка целая; тонкая линия — шов
- плитка с подрезкой (размер — на цепочке)
- ось старта; стрелки — направление укладки
- верх гидроизоляции: 200 от ЧП, в мокрой зоне — «до …»
- проём — не облицовывается
- сантехприбор: габарит, высота по практике
- короб инсталляции, в нём кнопка смыва 250×160
- вывод В1 (код — в ведомости привязок)
- вывод Т3 (код — в ведомости привязок)
- вывод К1 (код — в ведомости привязок)
- вывод за прибором / в коробе (не на сетке)
- электроточка: марка и H — по листам ЭОМ
- отметка уровня, м: ±0,000 — чистый пол 1-го этажа
- низ потолка; серая полоса — стена без плитки
- (А) обозначение стены А–Г (как на развёртках)

Примечания


1. Вид изнутри, стены по часовой стрелке А → Г. Высоты — от чистого пола (−0,015), отметки — от ±0,000 (чистый пол 1-го этажа). Раскладка от чистовых размеров (штукатурка 10 + клей 5 + плитка 9 мм), подрезки чистые; старт — от оси стены, ряды от пола целыми.
2. Облицовка не до потолка: верх плитки +2,389, выше — отделка стены по ведомости отделки до потолка +2,600; торец облицовки — профиль-окантовка.
3. Открытые выводы и электроточки — на шве или в центре плитки (допуск 10 мм; плитка от 900 мм по высоте — на шве или не ближе 60 мм к нему).
4. Выводы ВК стоят по оси прибора и с прибором не двигаются — привязки по «Плану выводов сантехники» без сдвига; вне сетки (Т3-1/В1-2, К1-2) — отверстие в плитке коронкой по той же привязке, плитку не сдвигать.
5. За приборами и в коробе (В1-1, К1-1) — штриховым кольцом.
6. Гидроизоляция: 200 мм от ЧП по периметру; углы — лентой; акт скрытых работ, пролив.
7. Короб 600×1200×250: лицо 600 мм от оси кнопки смыва, боковины, полка; углы — запил 45° или профиль; за коробом плитку не кладут.

	Лист	№ док.	Подпись	Дата
Дизайнер	Кырлан А.С.			04.11.26

Проект: Дом 120 м² — **М 1:25**

Раскладка плитки. Санузел гостевой. Развёртки стен

Стадия	Лист	Листов
П	38	136

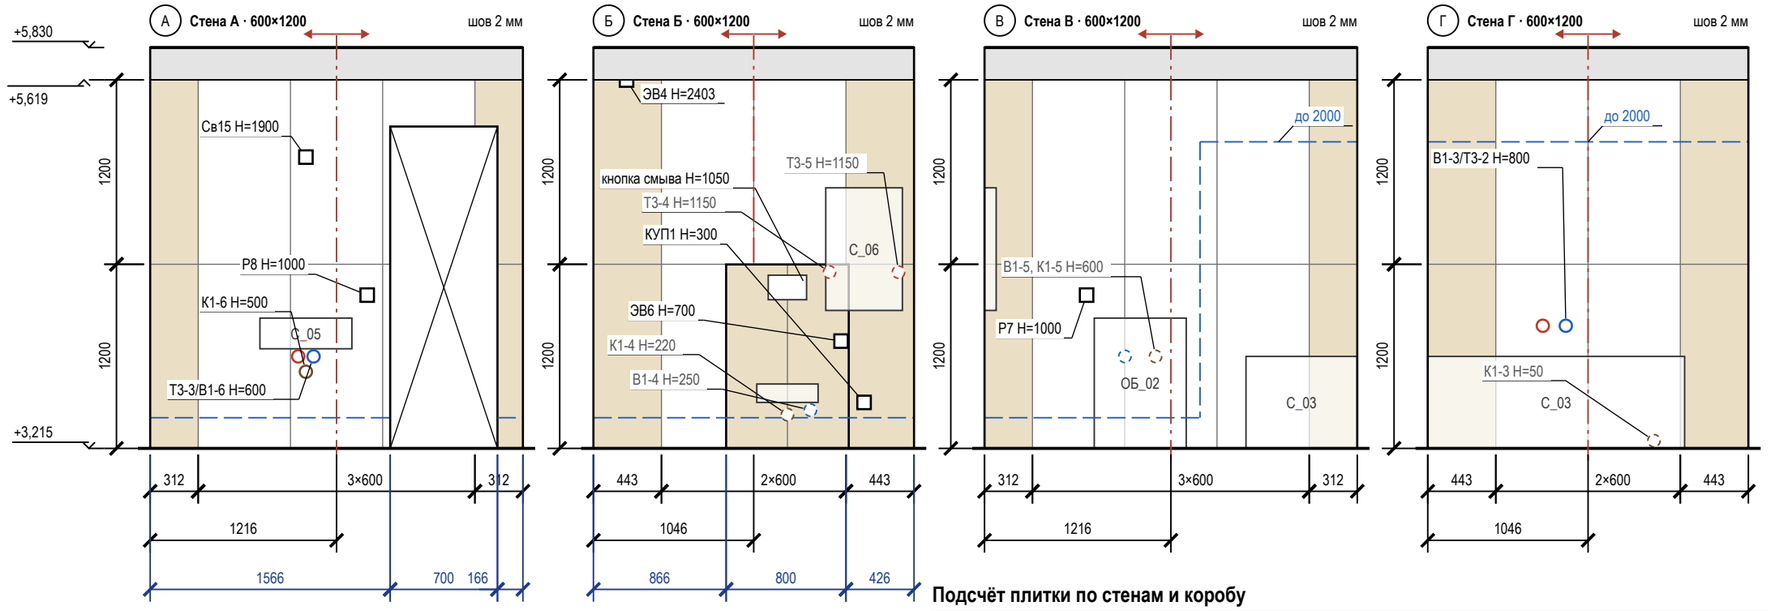

Подсчёт плитки по стенам и коробу

Поверхность	L × H, мм	S, м²	Целых	Подр.	С запасом	Подрезки: край / верх, мм
стена А	2432 × 2404	4,49	4	6	11	312 / 312; целый ряд
стена Б	2092 × 2404	4,18	2	5	8	443 / 443; целый ряд
короб (ст. Б)	800×1200×250	1,76	0	6	7	лицо 399 / 399; бок. 250
стена В	2432 × 2404	5,96	6	4	11	312 / 312; целый ряд
стена Г	2092 × 2404	3,46	4	4	9	443 / 443; целый ряд
Итого		**19,86**	**16**	**25**	**46**	

Сдвиг точек под раскладку

Точка (ВК, ЭОМ)	Стена	Проект: от угла / Н	Под раскладку: от угла / Н	Сдвиг, мм
Р8	А	1416 / 1000	1517 / 1000	+101 на шов
Св15	А	1016 / 1900	915 / 1900	−101 на шов
ЭВ4	Б	216 / 2403	143 / 2403	−73 в центр плитки
КУП1	Б	1766 / 300	1648 / 300	−118 на шов
ЭВ6	Б	1616 / 700	1648 / 700	+32 на шов
Р7	В	666 / 1000	614 / 1000	−52 в центр плитки


Условные обозначения

- плитка целая; тонкая линия — шов
- плитка с подрезкой (размер — на цепочке)
- ось старта; стрелки — направление укладки
- верх гидроизоляции: 200 от ЧП, в мокрой зоне — «до …»
- проём — не облицовывается
- сантехприбор: габарит, высота по практике
- короб инсталляции, в нём кнопка смыва 250×160
- вывод В1 (код — в ведомости привязок)
- вывод Т3 (код — в ведомости привязок)
- вывод К1 (код — в ведомости привязок)
- вывод за прибором / в коробе (не на сетке)
- электроточка: марка и Н — по листам ЭОМ
- отметка уровня, м: ±0,000 — чистый пол 1-го этажа
- низ потолка; серая полоса — стена без плитки
- (А) обозначение стены А–Г (как на развёртках)

Примечания

1. Вид изнутри, стены по часовой стрелке А → Г. Высоты — от чистого пола (+3,215), отметки — от ±0,000 (чистый пол 1-го этажа). Раскладка от чистовых размеров (штукатурка 10 + клей 5 + плитка 9 мм), подрезки чистые; старт — от оси стены, ряды от пола целыми.
2. Облицовка не до потолка: верх плитки +5,619, выше — отделка стены по ведомости отделки до потолка +5,830; торец облицовки — профиль-окантовка.
3. Точки из таблицы сдвигов переносятся до черновой разводки (ЭОМ — по тем же числам).
4. Выводы ВК стоят по оси прибора и с прибором не двигаются — привязки по «Плану выводов сантехники» без сдвига; вне сетки (Т3-3/В1-6, К1-6, В1-3/Т3-2) — отверстие в плитке коронкой по той же привязке, плитку не сдвигать.
5. За приборами и в коробе (В1-4, К1-4, Т3-4, Т3-5, В1-5, К1-5, К1-3) — штриховым кольцом.
6. Гидроизоляция: 200 мм от ЧП по периметру; над ванной — до 2000 и 300 мм за борт (СП 29.13330.2011, п. 7.2 — на высоту замачивания); углы — лентой; акт скрытых работ, пролив.
7. Короб 800×1200×250: лицо 399 / 399 мм от оси кнопки смыва, боковины, полка; углы — запил 45° или профиль; за коробом плитку не кладут.
8. Короб заходит на С_06 на 150 мм: сузить до 500 мм или сдвинуть прибор (решение дизайнера до закупки).


					Проект: Дом 120 м² — **М 1:40**
	Лист	№ док.	Подпись	Дата	Раскладка плитки. Санузел второго этажа. Развёртки стен
Дизайнер	Кырлан А.С.			04.11.26	Стадия: П · Лист: 39 · Листов: 136

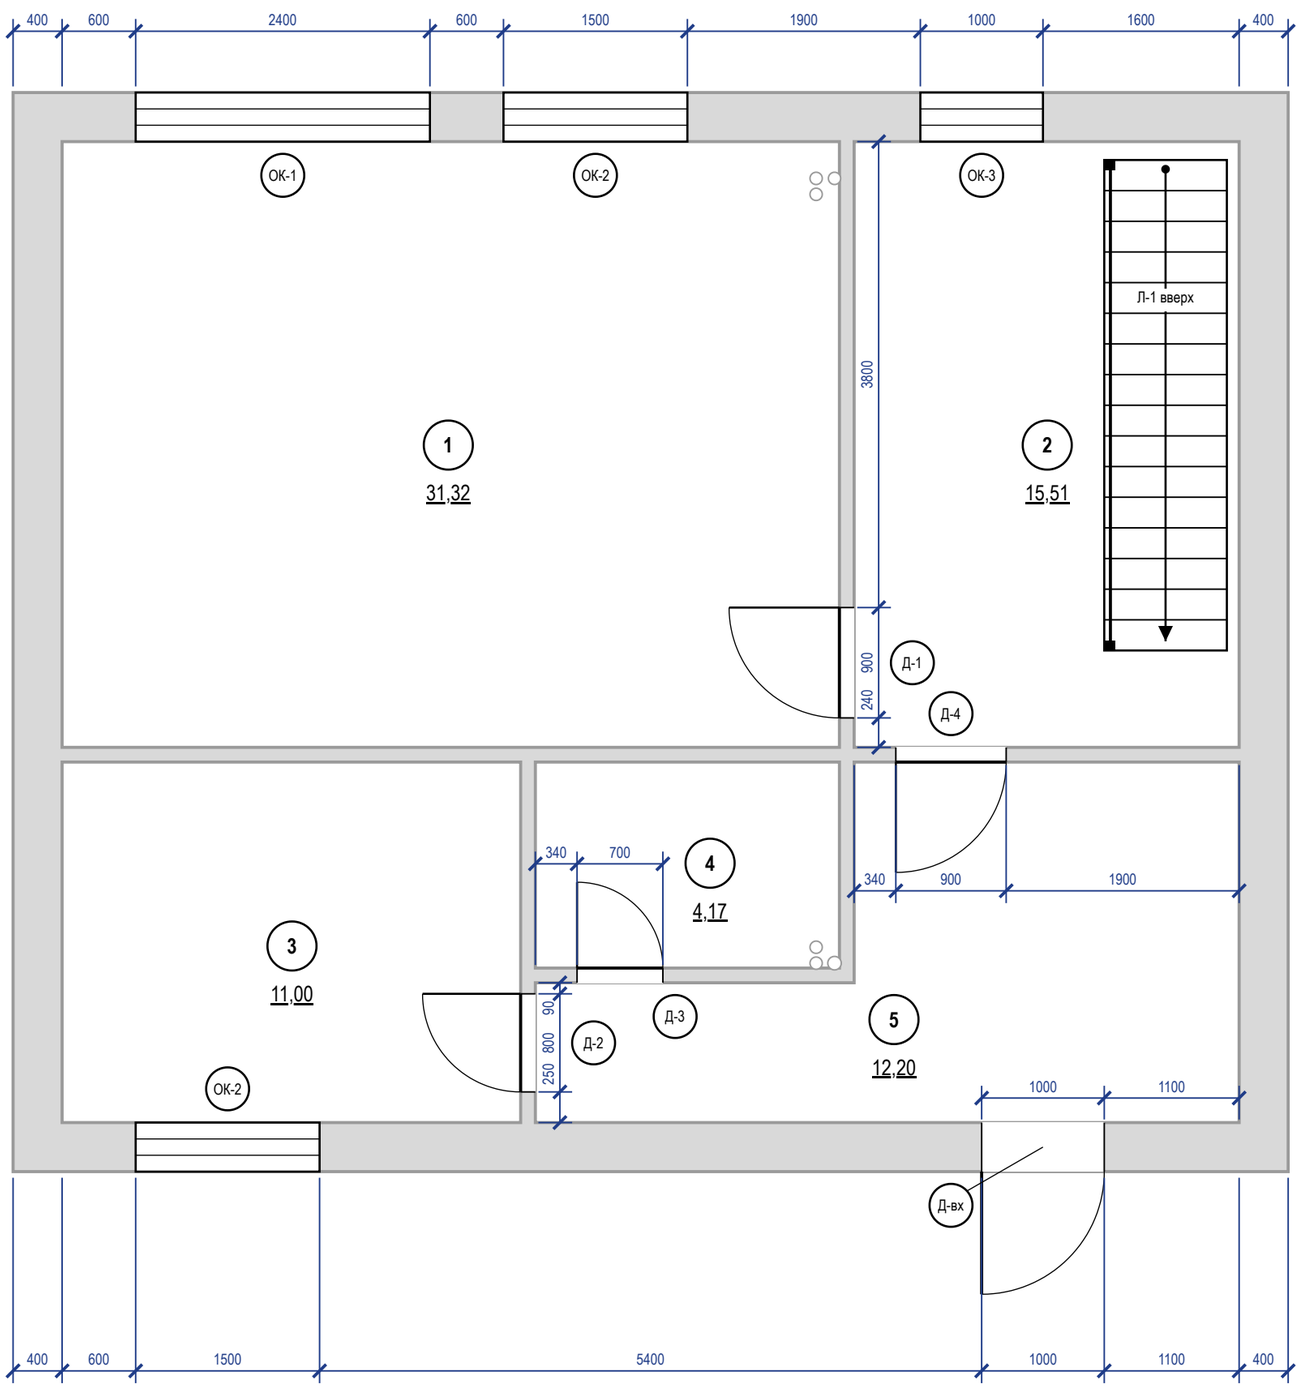

Примечания

1. Размеры проёмов и привязки — в миллиметрах от чистых граней стен до отделки; привязка — от угла того помещения, со стороны которого стоит размер. Размер проёма — ширина × высота от чистого пола 0,000. Размеры на плане — проёмов, не полотен: полотно — в ведомости, коробка — по системе. Откос от угла помещения до проёма с коробкой — не менее 50 мм.
2. Марки в кружках — типы заполнения проёмов (ГОСТ 21.501-2018, п. 5.3.2); одна марка — один типоразмер; количество сверено с планом.
3. Открывание: Л — петли слева, П — справа, если смотреть со стороны, куда открывается полотно (на себя).
4. Остекление окон: ОК-1 (пом. 1) — триплекс. Тип стекла указать при заказе оконных блоков; замена на другое стекло — только по согласованию с автором проекта.
5. ОК-1: низ остекления 500 мм — ниже 900 мм от чистого пола, поэтому окно заказывать с безопасным стеклом (триплекс); ограждение проёма в проекте не задано (СП 54.13330.2022, п. 6.4.9; ГОСТ Р 56926).
6. Скрытые двери (Д-1…Д-4): проём замерить в чистоте; блок заказать до штукатурки (≈ 30 дн.), короб ставить до штукатурки; полотно навесить после чистовой отделки, красить в цвет стен. Порядок практика монтажа, изготовитель подтверждает.
7. Д-1…Д-4 — существующие проёмы, до техзаключения не расширять.
8. Полотно «расч.» — по проёму и ряду изделия с запасом по каталогам, заказ — по таблице проёмов модели; Д-1…Д-4: проём 2100, а под полотно 2000 по каталогам нужен 2050–2080, под 2100 — 2150–2180: высоту проёма — по модели; Д-вх: входной блок по ГОСТ 31173-2016 — задать при выборе блока.
9. Ведомость заполнения проёмов — на весь дом, лист 41 (этаж «2-й этаж»); марки на всех этажах одни.

					Проект: Дом 120 м²		**М 1:50**
	Лист	№ док.	Подпись	Дата	План размещения дверей · 1-й этаж	Стадия	Лист	Листов
Дизайнер	Кырлан А.С.			04.11.26		П	40	136

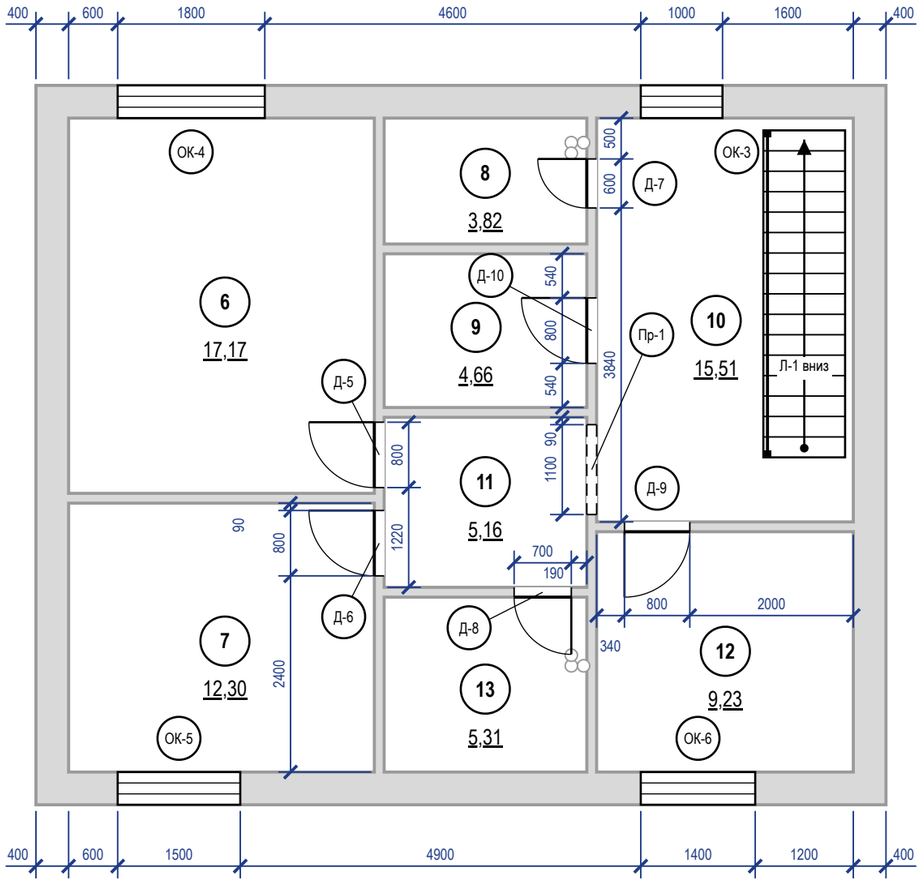

Ведомость заполнения проёмов (все этажи)


Марка	Наименование, обозначение	Проём ш×в, мм	Полотно (расч.)	Кол.	Откр.	Отделка полотна	Фурнитура	Прим.
Д-вх	Блок дверной входной, ГОСТ 31173-2016	1000×2100	блок задать	1	Л	в комплекте блока	в комплекте блока (замки, глазок)	пом. 5; наружу
Д-1	Дверь скрытого монтажа, UNION FILO-60 Piatto	900×2100	800×2000	1	Л	окраска G503 с двух сторон	скрытые петли 3D, магнитный замок	
Д-2	Дверь скрытого монтажа, UNION FILO-60 Piatto	800×2100	700×2000	1	Л	окраска G503 с двух сторон	скрытые петли 3D, магнитный замок	
Д-3	Дверь скрытого монтажа, UNION FILO-60 Piatto	700×2100	600×2000	1	П	в тон облицовки — пом. 4, G503 — пом. 5	скрытые петли 3D, магнитный замок, фиксатор WC	пом. 4; порог 15
Д-4	Дверь скрытого монтажа, UNION FILO-60 Piatto	900×2100	800×2000	1	Л	окраска G503 с двух сторон	скрытые петли 3D, магнитный замок	
Д-5	Дверь скрытого монтажа, UNION FILO-60 Piatto	800×2100	700×2000	1	Л	окраска G503 с двух сторон	скрытые петли 3D, магнитный замок	
Д-6	Дверь скрытого монтажа, UNION FILO-60 Piatto	800×2100	700×2000	1	Л	окраска G503 с двух сторон	скрытые петли 3D, магнитный замок	
Д-7	Дверь скрытого монтажа, UNION FILO-60 Piatto	600×2100	не задано (записи реестра нет)	1	Л	No. 222 — пом. 8, G503 — пом. 10	скрытые петли 3D, магнитный замок	
Д-8	Дверь скрытого монтажа, UNION FILO-60 Piatto	700×2100	600×2000	1	П	в тон облицовки — пом. 13, G503 — пом. 11	скрытые петли 3D, магнитный замок, фиксатор WC	пом. 13; порог 15
Д-9	Дверь скрытого монтажа, UNION FILO-60 Piatto	800×2100	700×2000	1	Л	окраска G503 с двух сторон	скрытые петли 3D, магнитный замок	
Д-10	Дверь скрытого монтажа, UNION FILO-60 Piatto	800×2100	700×2000	1	Л	S 0502-Y — пом. 9, G503 — пом. 10	скрытые петли 3D, магнитный замок	
Пр-1	Портал без заполнения	1100×2100		1				пом. 11; б/п
ОК-1	Блок оконный, ГОСТ 23166-2021; стекло — триплекс	2400×1900		1				пом. 1; низ 500
ОК-2	Блок оконный, ГОСТ 23166-2021	1500×1500		2				пом. 1, 3; низ 900
ОК-3	Блок оконный, ГОСТ 23166-2021	1000×1500		2				пом. 2, 10; низ 900
ОК-4	Блок оконный, ГОСТ 23166-2021	1800×1500		1				пом. 6; низ 900
ОК-5	Блок оконный, ГОСТ 23166-2021	1500×1450		1				пом. 7; низ 900
ОК-6	Блок оконный, ГОСТ 23166-2021	1400×1450		1				пом. 12; низ 900

Примечания


1. Размеры проёмов и привязки — в миллиметрах от чистых граней стен до отделки; привязка — от угла того помещения, со стороны которого стоит размер. Размер проёма — ширина × высота от чистого пола 0,000. Размеры на плане — проёмов, не полотен: полотно — в ведомости, коробка — по системе. Откос от угла помещения до проёма с коробкой — не менее 50 мм.
2. Марки в кружках — типы заполнения проёмов (ГОСТ 21.501-2018, п. 5.3.2); одна марка — один типоразмер; количество сверено с планом.
3. Открывание: Л — петли слева, П — справа, если смотреть со стороны, куда открывается полотно (на себя).
4. Скрытые двери (Д-5…Д-10): проём замерить в чистоте; блок заказать до штукатурки (≈ 30 дн.), короб ставить до штукатурки; полотно навесить после чистовой отделки, красить в цвет стен. Порядок — практика монтажа, изготовитель подтверждает.
5. Д-5…Д-10 — существующие проёмы, до техзаключения не расширять.
6. Полотно «расч.» — по проёму и ряду изделия с запасом по каталогам, заказ — по таблице проёмов модели; Д-5, Д-6, Д-8…Д-10: проём 2100, а под полотно 2000 по каталогам нужен 2050–2080, под 2100 — 2150–2180: высоту проёма — по модели; Д-7: проём 600×2100 вне ряда полотен изделия — полотно задать при выборе модели.
7. Ведомость заполнения проёмов — на весь дом, количество по обоим этажам; марки на плане этажа «1-й этаж» (лист 40) по этой ведомости.
8. Привязка проёма к углу помещения меньше 1 мм на листе, размер на плане не показан: Д-5 — 60 мм.

					Проект: Дом 120 м²	М 1:75
	Лист	№ док.	Подпись	Дата		
Дизайнер	Кырлан А.С.			04.11.26	План размещения дверей · 2-й этаж	Стадия: П; Лист: 41; Листов: 136

План марша Л-1 (М 1:50) · 2. Холл с лестницей

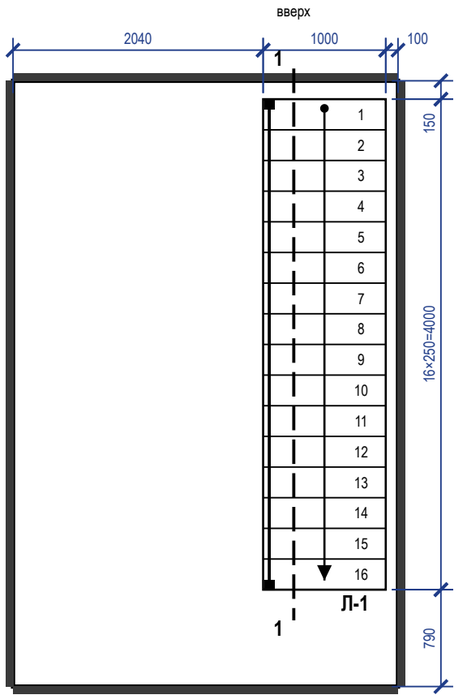


Разрез 1-1 (М 1:50)

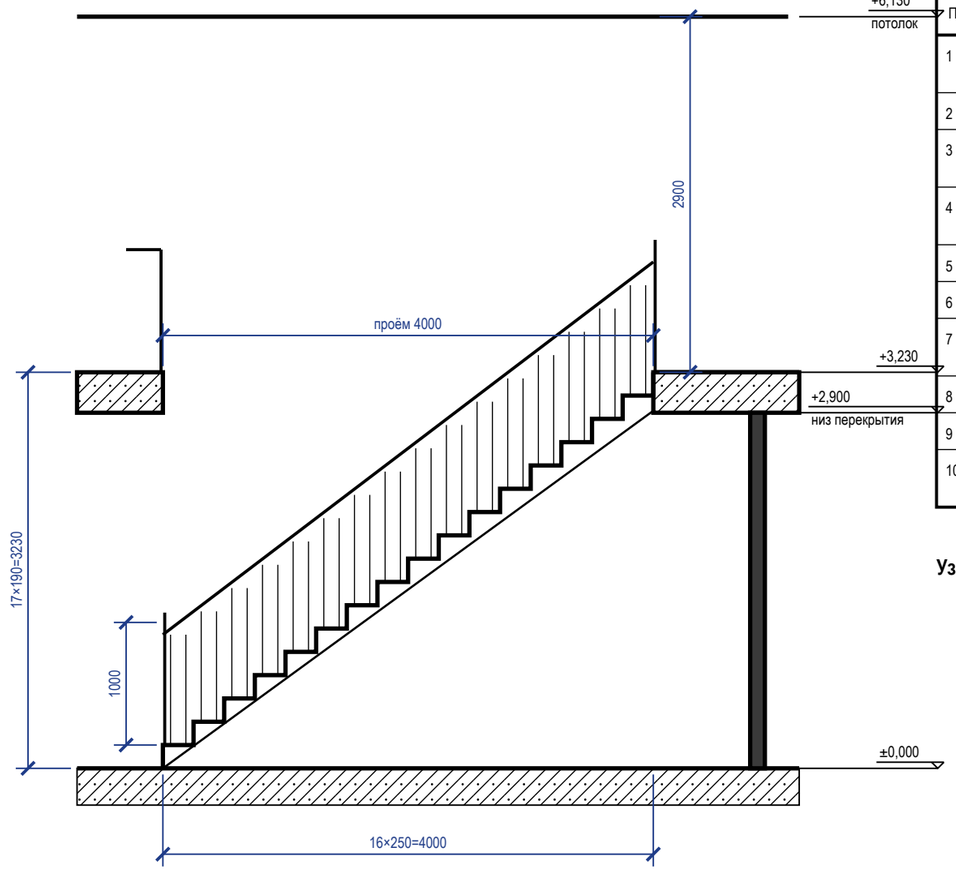

Спецификация элементов лестницы Л-1

Поз.	Наименование	Кол.	Материал, сечение	Примечание
1	Ступень (проступь)	16	дуб табак, 40 мм	1000×250, толщина по изделию
2	Подступенок	17	дуб табак	высота 190
3	Косоур	2	косоуры стальные, тёплый графит	несущие марша
4	Столб ограждения марша	2	дуб табак, стойки — графит	по концам марша, стороны Г
5	Балясина	45	дуб табак, стойки — графит	шаг 110, просвет 80
6	Поручень марша	1	Ø40	L ≈ 5,02 м, h 900
7	Столб ограждения проёма	2	дуб табак, стойки — графит	углы проёма, стороны Г
8	Балясина ограждения проёма	36	дуб табак, стойки — графит	шаг 110
9	Поручень ограждения проёма	1	Ø40	L ≈ 4,00 м, h 1000
10	Крепёж ограждения	1	комплект по изделию	нагрузка на поручень 0,5 кН/м

Узел 1. Крепление стойки ограждения (М 1:5)

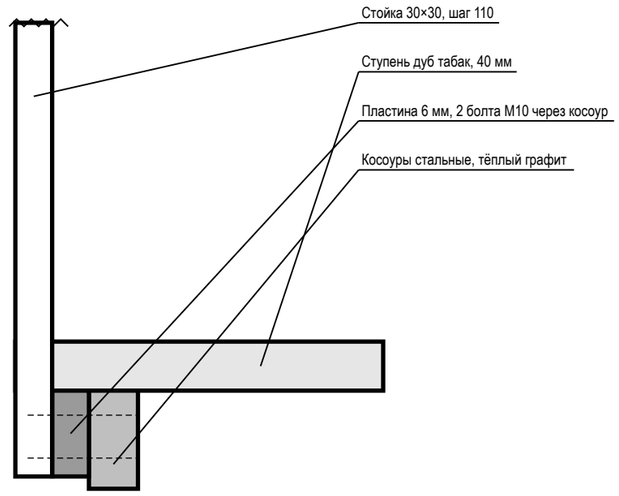


Зазор от низа заполнения до ступени — не более 100 (ГОСТ 25772-2025, прил. А, прим. 3)

Примечания

1. Лестница Л-1: 17 подъёмов × 190 мм = 3230 мм (отм. ±0,000 … +3,230), проступь 250 мм, ширина марша 1000 мм; уклон 37,2°, шаг 2h + b = 630 мм (удобно 600–640 — практика).
2. Ограждение марша со стороны Г: балясины, просвет между элементами 80 мм (не больше 150 — ГОСТ 25772-2025, табл. 3, тип МВ); высота 1000 мм, поручень с одной стороны на 900 мм по линии носков (не менее 900 — СП 55.13330.2016, п. 8.3; СП 59.13330.2020, п. 6.2.11).
3. Проём в перекрытии 1000×4000 мм на этаже 2 ограждён со сторон Г высотой 1000 мм, непрерывно, с поручнем (СП 55.13330.2016, п. 8.3); нагрузка на поручень 0,5 кН/м (СП 20.13330.2016, п. 8.2.6).
4. Просвет над линией носков — не менее 2900 мм (ступень 17, под потолком мансарды); рекомендуется не менее 2000, путь эвакуации — 2200 (СП 55.13330.2016, п. 7.4).
5. Все подступенки одной высоты (СП 55.13330.2016, п. 8.2). Разность отметок чистых полов замерить до заказа изделия: высота подступенка — по замеру.
6. Узел 1 — типовое решение крепления стойки к косоуру; крепёж, сечения и материал — по проекту изделия изготовителя лестницы.

					Проект: Дом 120 м² — **М 1:50**
	Лист	№ док.	Подпись	Дата	
Дизайнер	Кырлан А.С.			04.11.26	Лестница Л-1
					Стадия: П · Лист: 42 · Листов: 136

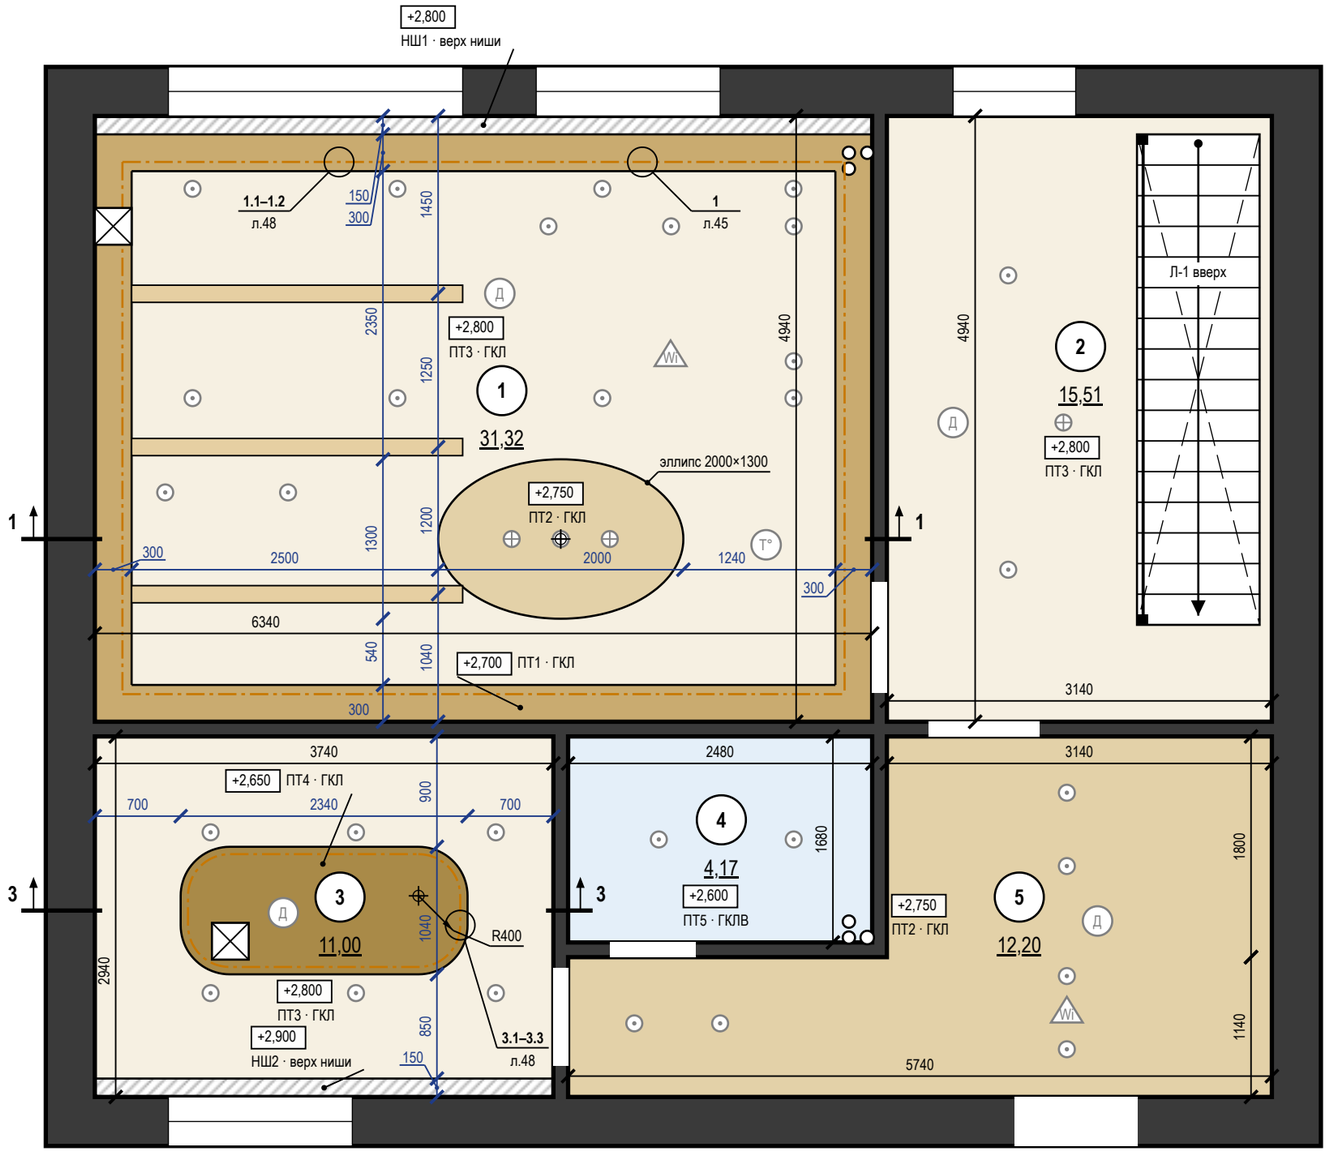

Ведомость потолков

Пом.	Марка	Конструкция	Низ / верх ниши	S, м²	Q
1	ПТ1	ГКЛ П113, короб LED	+2,700	6,32	Q3
1	ПТ2	ГКЛ П113, эллипс	+2,750	2,04	Q3
1	ПТ3	ГКЛ П113	+2,800	22,01	Q3
1	НШ1	ниша под шторы 150×100	+2,800	0,95	
2	ПТ3	ГКЛ П113	+2,800	11,51	Q3
3	ПТ4	ГКЛ П113, остров + LED	+2,650	2,30	Q3
3	ПТ3	ГКЛ П113	+2,800	8,14	Q3
3	НШ2	ниша под шторы 150×100	+2,900	0,56	
4	ПТ5	ГКЛВ П113	+2,600	4,17	Q3
5	ПТ2	ГКЛ П113	+2,750	12,20	Q3
		Итого		**70,20**	


Ведомость вырезов и закладных в потолке

Марка	Устройство	Кол.	Пом.
	Светильник встраиваемый (марки — план освещения)	30	1, 2, 3, 4, 5
	Светильник подвесной (марки — план освещения)	4	1, 2
ИП4, ИП6, ИП2, ИП3	Извещатель дымовой	4	1, 2, 3, 5
ИП5	Извещатель тепловой	1	1
АР2, АР1	Точка доступа Wi-Fi, PoE	2	1, 5
	Люк ревизии 300×300	2	1, 3

Примечания

1. За отметку ±0,000 принят уровень чистого пола сухих помещений 1-го этажа (готовое покрытие), а не существующего пола; пол пом. 4 — −0,015; верх плиты перекрытия −0,064 — расчётный по пирогу пола, не замерен; существующий пол снимается до плиты, его отметка не замерена. Отметки в прямоугольниках — низ потолка; низ перекрытия +2,900. Марка потолка — одна конструкция и отметка на весь альбом.
2. Потолки ГКЛ — каркасная система П113: подвесы через 1000 (с запасом: СП 163, табл. 14 — до 1100 при 0,15 кН/м²), несущие профили через 500, основные через 1200 мм; листы — поперёк несущих профилей. В помещениях 4 — ГКЛВ на оцинкованном каркасе.
3. Нижний уровень — пояс-короб по периметру шириной 300 мм (карниз подсветки + 150 мм полки), верхний — поле внутри пояса: пом. 1.
4. LED-лента в алюминиевом профиле посередине карниза короба шириной 300 мм (узел 1, лист 45); длина по плану: пом. 1 — 20,5 м (в плане освещения 20,5).
5. Балки декоративные 140×100 мм, фальш-балка, массив сосны, белёная (известковая морилка): пом. 1 — 3 шт., 8,1 м, низ +2,700; крепление — на закладной брус 50×50 к каркасу П113, саморезы скрыто.
6. Ниши под шторы 150×100 мм — на всю длину стены с окном; карниз — на закладной до обшивки (узел 2 — пом. 1, лист 45; узел 4 — пом. 3, лист 47).
7. Светильники и потолочные устройства — подложка с планов освещения, слаботочных систем и вентиляции (положение — по ним); вырезы и закладные — по ведомости на листе, до обшивки; отверстия не совмещать с профилями, глубина корпуса светильника до 70 мм.
8. Разрезы 1–1 — лист 45; 3–3 — лист 46; высоты мебели и дверных блоков сверены с низом потолка в разрезах; гибка бортов фигур и ленты ниш — там же; размеры фигурных уровней — фрагменты 1 (лист 46); 2 (лист 47).
9. Шпаклевание ГКЛ и условия приёмки — Q3: рассеянный дневной свет, осмотр с 2 м; боковой свет не оценивается.
10. Люки ревизии 300×300 мм — по центру блоков питания LED (БП4, БП2; координаты — план освещения).
11. Пом. 2: над маршем лестницы Л-1 — проём перекрытия 1000×4000 мм; потолок ГКЛ по кромке проёма закрыт бортом до перекрытия (ГКЛ по ПН 28×27, длина кромки 10,0 м); светильники и устройства в проёме не ставятся.

					Проект: Дом 120 м² — **М 1:50**
	Лист	№ док.	Подпись	Дата	План потолков · 1-й этаж — Стадия: П; Лист: 43; Листов: 136
Дизайнер	Кырлан А.С.			04.11.26	

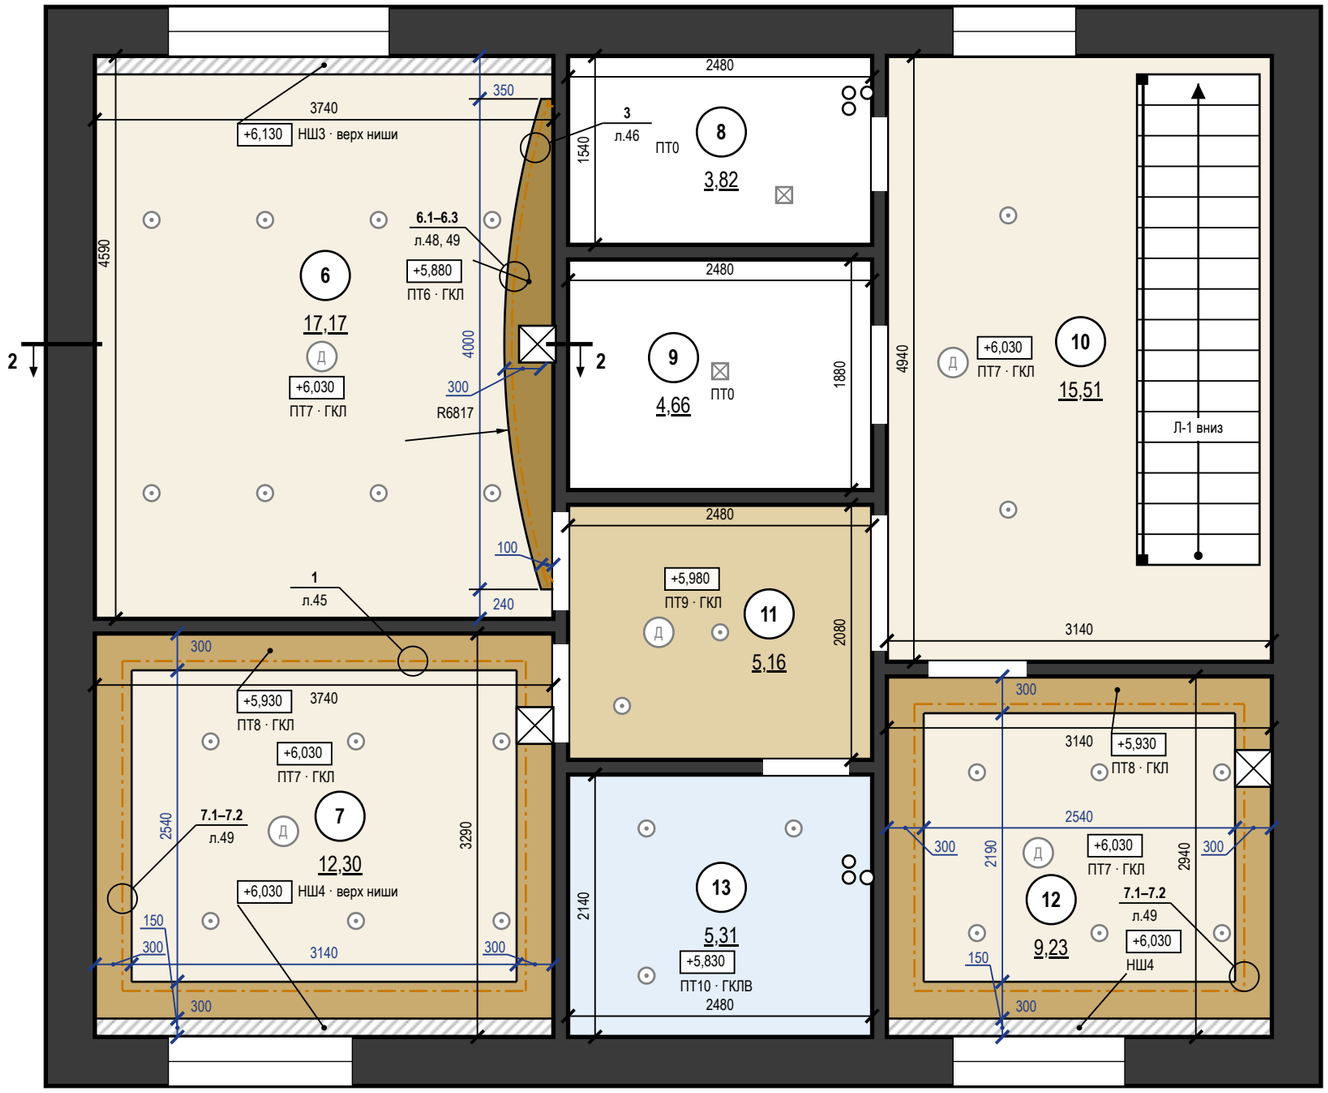

Ведомость потолков

Пом.	Марка	Конструкция	Низ / верх ниши	S, м²	Q
6	ПТ6	ГКЛ П113, дуга + LED	+5,880	1,20	Q3
6	ПТ7	ГКЛ П113	+6,030	15,41	Q3
6	НШ3	ниша под шторы 150×100	+6,130	0,56	
7	ПТ8	ГКЛ П113, короб LED	+5,930	3,77	Q3
7	ПТ7	ГКЛ П113	+6,030	7,97	Q3
7	НШ4	ниша под шторы 150×100	+6,030	0,56	
8, 9	ПТ0	Потолок под покраску	+6,130	8,48	
10	ПТ7	ГКЛ П113	+6,030	15,51	Q3
11	ПТ9	ГКЛ П113	+5,980	5,16	Q3
12	ПТ8	ГКЛ П113, короб LED	+5,930	3,20	Q3
12	ПТ7	ГКЛ П113	+6,030	5,56	Q3
12	НШ4	ниша под шторы 150×100	+6,030	0,47	
13	ПТ10	ГКЛВ П113	+5,830	5,31	Q3
		Итого		**73,16**	

Ведомость вырезов и закладных в потолке

Марка	Устройство	Кол.	Пом.
	Светильник встраиваемый (марки — план освещения)	27	6, 7, 10, 11, 12, 13
	Светильник накладной (марки — план освещения)	2	8, 9
ИП1, ИП8, ИП9, ИП7, ИП10	Извещатель дымовой	5	6, 7, 10, 11, 12
	Люк ревизии 300×300	3	6, 7, 12

Примечания

1. За отметку ±0,000 принят уровень чистого пола 1-го этажа (готовое покрытие), а не существующего пола; чистый пол сухих помещений этажа — +3,230; пол пом. 13 — +3,215; верх плиты перекрытия +3,166 — расчётный по пирогу пола, не замерен; существующий пол снимается до плиты, его отметка не замерена. Отметки в прямоугольниках — низ потолка; низ перекрытия +6,130. Марка потолка одна конструкция и отметка на весь альбом.
2. Потолки ГКЛ — каркасная система П113: подвесы через 1000 (с запасом: СП 163, табл. 14 — до 1100 при 0,15 кН/м²), несущие профили через 500, основные через 1200 мм; листы — поперёк несущих профилей. В помещениях 13 — ГКЛВ на оцинкованном каркасе.
3. Нижний уровень — пояс-короб по периметру шириной 300 мм (карниз подсветки + 150 мм полки), верхний — поле внутри пояса: пом. 7, 12.
4. LED-лента в алюминиевом профиле посередине карниза короба шириной 300 мм (узел 1, лист 45); длина по плану: пом. 7 — 12,0 м (в плане освещения 12); пом. 12 — 10,1 м (в плане освещения 10,1).
5. Ниши под шторы 150×100 мм — на всю длину стены с окном; карниз — на закладной до обшивки (узел 4 — пом. 6, лист 47; узел 2 — пом. 7, 12, лист 45).
6. Светильники и потолочные устройства — подложка с планов освещения, слаботочных систем и вентиляции (положение — по ним); вырезы и закладные — по ведомости на листе, до обшивки; отверстия не совмещать с профилями, глубина корпуса светильника до 70 мм.
7. Разрезы 2–2 — на листе 45; высоты мебели и дверных блоков сверены с низом потолка в разрезах; гибка бортов фигур и ленты ниш — там же; размеры фигурных уровней — фрагмент 3 (лист 47).
8. Шпаклевание ГКЛ и условия приёмки — Q3: рассеянный дневной свет, осмотр с 2 м; боковой свет не оценивается.
9. Люки ревизии 300×300 мм — по центру блоков питания LED (БП1, БП6, БП7; координаты — план освещения).
10. ПТ0 — пом. 8, 9: потолок под покраску, без подвесного потолка, низ +6,130; материал и цвет — по ведомости отделки.
11. Основание потолка ПТ0 — по проекту КР дома: конструкция перекрытия в исходных данных не задана.

	Лист	№ док.	Подпись	Дата
Дизайнер	Кырлан А.С.			04.11.26


Проект: Дом 120 м² — **М 1:50**

План потолков · 2-й этаж

Стадия	Лист	Листов
П	44	136


Разрез 1–1 (М 1:40)

Пом. 1 Гостиная-кухня

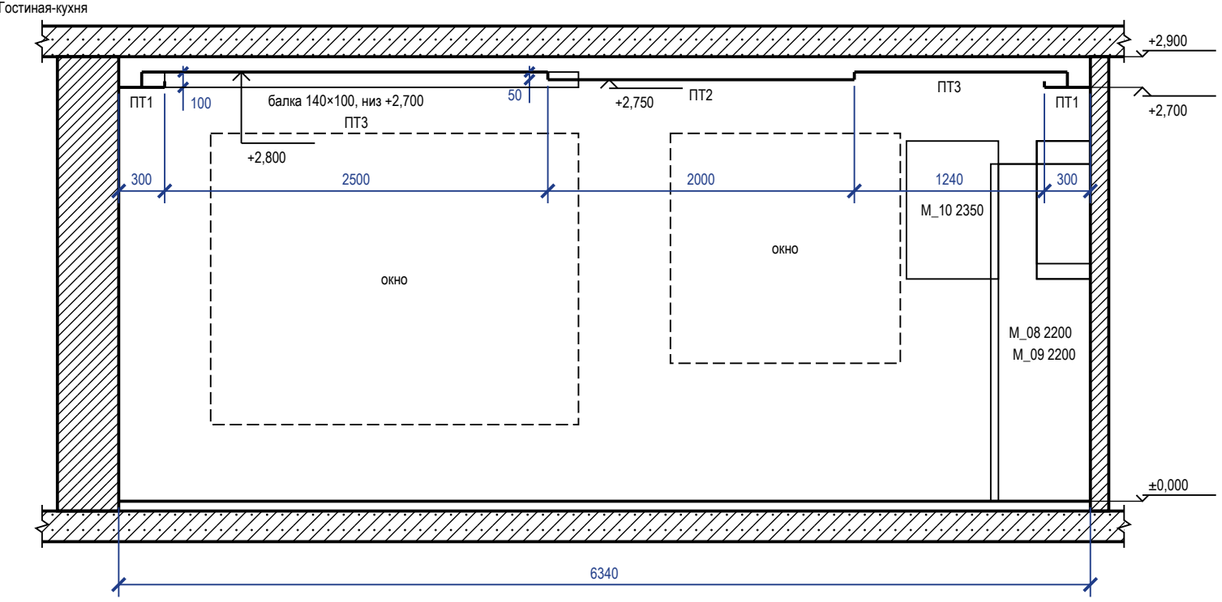


Разрез 2–2 (М 1:40)

Пом. 6 Спальня родителей

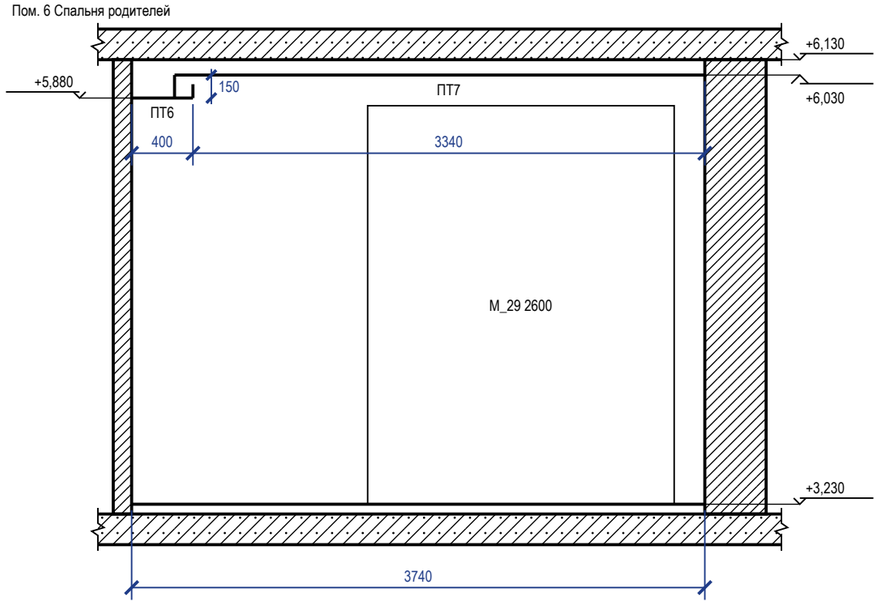

1 Короб с LED-подсветкой (М 1:10)


Пом. 1, 7, 12; карниз 150×100, щель под свет 60 мм

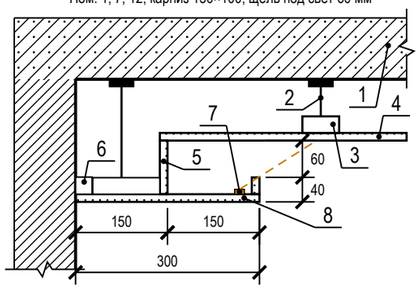

1 — плита перекрытия
2 — подвес прямой, шаг 1000 мм
3 — ПП 60×27: несущие через 500, основные через 1200 мм
4 — ГКЛ 12,5 по П113 — верхний уровень
5 — задняя стенка и бортик карниза — ГКЛ 12,5
6 — ПН 28×27 по периметру, к стене через 500 мм
7 — LED-лента в алюминиевом профиле
8 — низ короба — ГКЛ 12,5 по ПП 60×27

2 Ниша под шторы (М 1:10)

Пом. 1, 7, 12; без подсветки; закладные под карниз — до обшивки

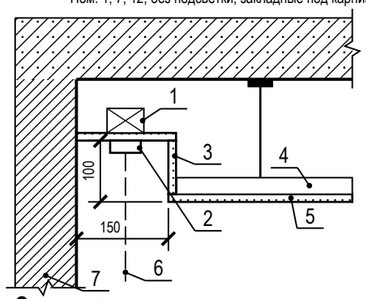

1 — закладная под карниз — брус 40×50
2 — карниз (шина), высота с верхом портьеры 80 мм
3 — стенка и потолок ниши — ГКЛ 12,5
4 — ПП 60×27 — каркас короба
5 — низ короба нижнего уровня — ГКЛ 12,5
6 — портьера
7 — стена с окном

Условные обозначения

- плита перекрытия в сечении
- стена в сечении
- потолок ГКЛ в сечении; под линией — марка потолка (план потолков)
- мебель и дверные проёмы за секущей плоскостью; число — марка и верх от чистого пола, мм
- балка декоративная: в сечении — заливка, за плоскостью — тонкой линией; низ балки — подписью у балки или отметкой справа

Отметки по помещениям, м

Пом.	низ короба	верх. уровень	низ перекрытия
1	+2,700	+2,800	+2,900
7, 12	+5,930	+6,030	+6,130

Отметки по помещениям, м

Пом.	низ потолка	верх ниши	низ перекрытия
1	+2,700	+2,800	+2,900
7, 12	+5,930	+6,030	+6,130


Примечания

1. Разрезы — по линиям 1–1, 2–2 на плане потолков. Отметки — от ±0,000 (чистый пол 1-го этажа), м; размеры — мм.
2. Высоты мебели и дверных блоков за секущей плоскостью сверены с низом потолка над ними: верх ниже низа короба и поля.
3. ГКЛ 12,5 мм по каркасу П113; перепад уровней и бортик карниза — ГКЛ по ПП 60×27 (узел 1 — на этом листе). Ниша под шторы — на всю длину стены с окном, карниз на закладной до обшивки (узел 2 — на этом листе; узел 4 — лист 47).
4. Толщины плит перекрытия и пирога пола показаны условно.
5. Сечения потолков по помещениям М 1:10 (отметки помещения, профили, подвесы, крепёж, изделия) — листы 48–49.
6. Ведомость объёмов потолков (лист ГКЛ, профиль, подвесы, лента, блоки питания, люки) — на листе 47.
7. Фрагменты 1, 3, 2 — помещения с фигурными уровнями (размеры фигур, радиусы, отметки) — на листах 46, 47.

					Проект: Дом 120 м²	М 1:40; 1:10
	Лист	№ док.	Подпись	Дата		
Дизайнер	Кырлан А.С.			04.11.26	Разрезы и узлы потолков	Стадия: П; Лист: 45; Листов: 136


Разрез 3–3 (М 1:40)

Пом. 3 Кабинет

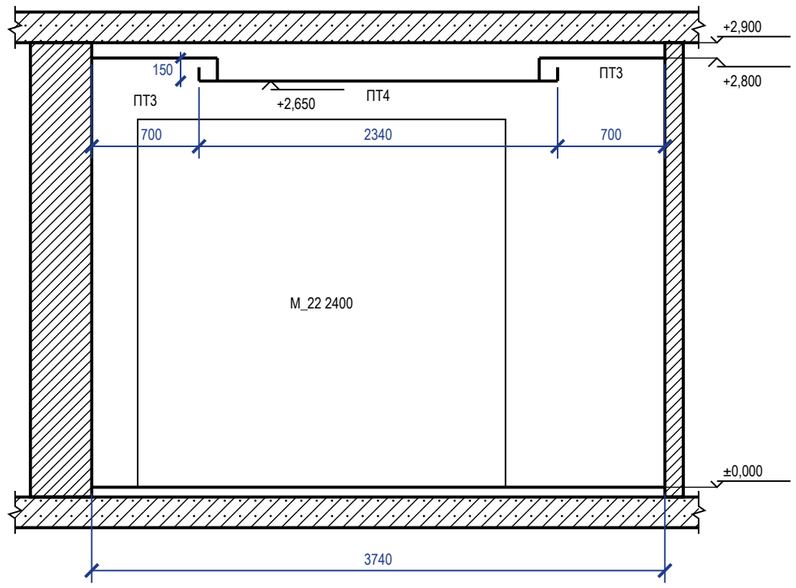

Фрагмент 1. Пом. 1 Гостиная-кухня — уровни потолка (М 1:50)

Цепочки — от чистых граней стен; отметки — низ уровня от ±0,000

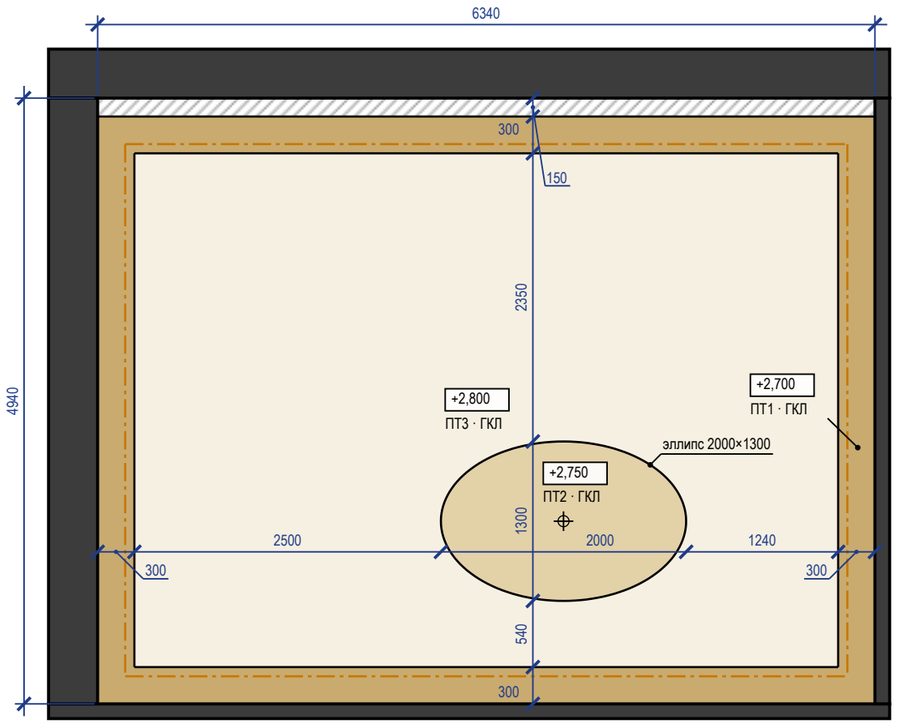


ПТ1 — низ +2,700 · ПТ2 — низ +2,750 · ПТ3 — низ +2,800

LED-лента в нише подсветки (карниз короба, ниша фигуры) · ниша под шторы

3 Ниша LED фигурного уровня (М 1:10)

Пом. 3, 6; карниз 120×100, щель под свет 60 мм

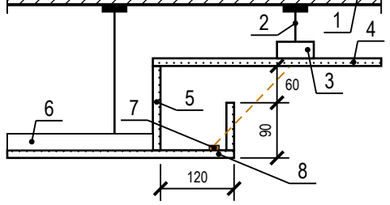

1 — плита перекрытия
2 — подвес прямой, шаг 1000 мм
3 — ПП 60×27: несущие через 500, основные через 1200 мм
4 — ГКЛ 12,5 по П113 — верхний уровень
5 — задняя стенка и бортик карниза — ГКЛ 12,5
6 — ПП 60×27 каркаса нижнего уровня, ПН по контуру фигуры (на дуге — с надрезами)
7 — LED-лента в алюминиевом профиле
8 — низ короба — ГКЛ 12,5 по ПП 60×27

Отметки по помещениям, м

Пом.	низ короба	верх. уровень	низ перекрытия
3	+2,650	+2,800	+2,900
6	+5,880	+6,030	+6,130

Примечания

1. Разрезы — по линиям 3–3 на плане потолков. Отметки — от ±0,000 (чистый пол 1-го этажа), м; размеры — мм.
2. Высоты мебели и дверных блоков за секущей плоскостью сверены с низом потолка над ними: верх ниже низа короба и поля.
3. ГКЛ 12,5 мм по каркасу П113; узлы коробов и ниш под шторы: узел 1 — лист 45; узел 2 — лист 45; узел 4 — лист 47; условные обозначения разрезов — на листе 45.
4. Толщины плит перекрытия и пирога пола показаны условно.
5. Фрагмент 1 — фигурные уровни потолка крупно: привязки краёв и центров фигур к чистым граням стен, радиусы (R) с центрами, хорда и стрелка дуги, отметки низа каждого уровня; цвета уровней — как на плане потолков.
6. Фигурные уровни: борт — ГКЛ по ПН с надрезами (на дуге шаг стоек борта 300 мм при R до 2500, 400 — до 5000) или по гнутому заводскому профилю (СП 163, 6.3.3); гибка: эллипс пом. 1 R423 — ГКЛ 6,5 мокрой гибкой; остров пом. 3 R400 — ГКЛ 6,5 мокрой гибкой; дуга пом. 6 R6817 — ГКЛ 12,5 сухой гибкой (СП 163, табл. 9). Лента в нише фигуры по оси: остров пом. 3 — 5,7 м, дуга пом. 6 — 4,5 м; узел ниши LED фигуры: узел 3 — на этом листе — пом. 3, 6.

	Лист	№ док.	Подпись	Дата
Дизайнер	Кырлан А.С.			04.11.26


Проект: Дом 120 м² — **М 1:40; 1:50; 1:10**

Разрезы и узлы потолков (продолжение)

Стадия	Лист	Листов
П	46	136

Фрагмент 3. Пом. 6 Спальня родителей — уровни потолка (М 1:50)

Цепочки — от чистых граней стен; отметки — низ уровня от ±0,000

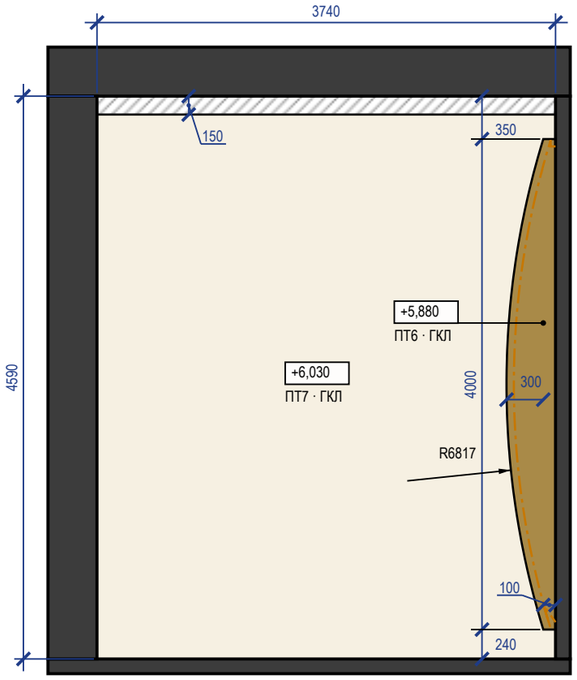


ПТ6 — низ +5,880 · ПТ7 — низ +6,030 · LED-лента в нише подсветки (карниз короба, ниша фигуры) · ниша под шторы

Ведомость объёмов потолков

Позиция	Ед.	Кол.	Пом.
Лист ГКЛ 12,5	м²	143,72	1, 2, 3, 5, 6, 7, 10, 11, 12
Лист ГКЛВ 12,5	м²	9,48	4, 13
Лист ГКЛ арочный 6,5	м²	1,73	1, 3
Борта и карнизы (входят в площади листов выше)	м²	19,19	1, 2, 3, 6, 7, 12
Профиль ПП 60×27	м	405,38	1, 2, 3, 4, 5, 6, 7, 10, 11, 12, 13
Профиль ПН 28×27	м	381,88	1, 2, 3, 4, 5, 6, 7, 10, 11, 12, 13
Подвес прямой	шт.	167	1, 2, 3, 4, 5, 6, 7, 10, 11, 12, 13
Анкер-клин к плите	шт.	167	1, 2, 3, 4, 5, 6, 7, 10, 11, 12, 13
Шуруп TN 3,5×25	шт.	3544	1, 2, 3, 4, 5, 6, 7, 10, 11, 12, 13
Лента армирующая для швов	м	184,88	1, 2, 3, 4, 5, 6, 7, 10, 11, 12, 13
Шпаклёвка для швов	кг	61,63	1, 2, 3, 4, 5, 6, 7, 10, 11, 12, 13
Грунтовка (швы)	л	15,41	1, 2, 3, 4, 5, 6, 7, 10, 11, 12, 13
Лента разделительная по периметру	м	155,16	1, 2, 3, 4, 5, 6, 7, 10, 11, 12, 13
Сплошная шпаклёвка и окраска (площадь развёртки)	м²	154,07	1, 2, 3, 4, 5, 6, 7, 10, 11, 12, 13
Лента LED	м	52,67	1, 3, 6, 7, 12
Требуемая мощность блоков питания	Вт	657	1, 3, 6, 7, 12
Установленная мощность блоков питания	Вт	1100	1, 3, 6, 7, 12
Блок питания LED	шт.	5	1, 3, 6, 7, 12
Люк ревизии	шт.	5	1, 3, 6, 7, 12

Фрагмент 2. Пом. 3 Кабинет — уровни потолка (М 1:50)


Цепочки — от чистых граней стен; отметки — низ уровня от ±0,000

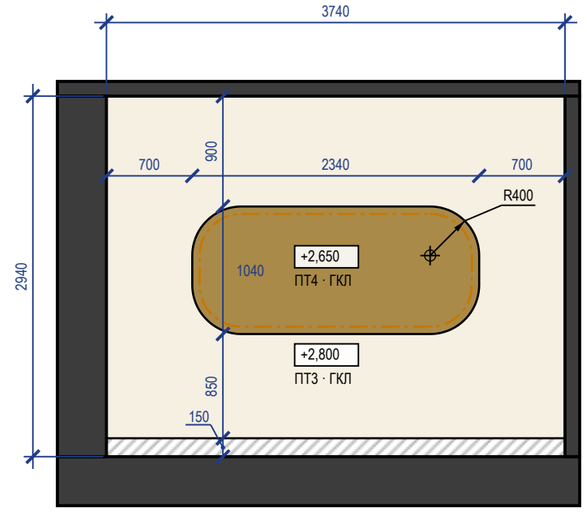

ПТ4 — низ +2,650 · ПТ3 — низ +2,800 · LED-лента в нише подсветки (карниз короба, ниша фигуры) · ниша под шторы

4 Ниша под шторы (М 1:10)

Пом. 3, 6; без подсветки; закладные под карниз — до обшивки

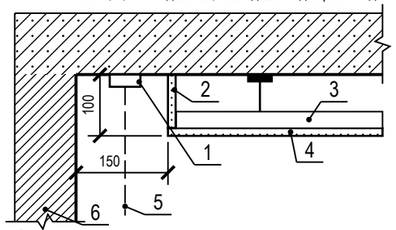

1 — карниз (шина), высота с верхом портьеры 80 мм
2 — стенка ниши — ГКЛ 12,5
3 — ПП 60×27 — каркас короба
4 — низ короба нижнего уровня — ГКЛ 12,5
5 — портьера
6 — стена с окном

Отметки по помещениям, м

Пом.	низ потолка	верх ниши	низ перекрытия
3	+2,800	+2,900	+2,900
6	+6,030	+6,130	+6,130


Примечания

1. ГКЛ 12,5 мм по каркасу П113; узлы коробов и ниш под шторы: узел 1 — лист 45; узел 2 — лист 45; узел 4 — на этом листе; условные обозначения разрезов — на листе 45.
2. Фрагменты 3, 2 — фигурные уровни потолка крупно: привязки краёв и центров фигур к чистым граням стен, радиусы (R) с центрами, хорда и стрелка дуги, отметки низа каждого уровня; цвета уровней как на плане потолков.
3. Ведомость объёмов — по геометрии плана потолков: Лист ГКЛ 12,5 — плоскости уровней + борта (без арочных участков); Лист ГКЛВ 12,5 — плоскости уровней + борта; Лист ГКЛ арочный 6,5 — кривая борта × высота борта и стенки ниши × 2 слоя (R423 мокрая гибка, R400 мокрая гибка); Борта и карнизы — длина перепада × перепад; Профиль ПП 60×27 — S × (1/шаг несущ. + 1/шаг осн.) + стойки бортов; Профиль ПН 28×27 — периметр стен + 2 × перепады + карнизы; Подвес прямой — по раскладке: S уровня / (шаг осн. × шаг подвесов), пояс уже шага — ряд вдоль пояса, фигура — по контуру; шаг подвесов — не больше табл. 14 СП 163; Анкер-клин к плите — по одному на подвес (Knauf П113); Шуруп TN 3,5×25 — 23 шт./м² (Knauf П113, табл. 2 альбома П 11); Лента армирующая для швов 1,2 м/м² листа (Knauf); Шпаклёвка для швов — 0,4 кг/м² листа, только швы (Knauf); Грунтовка (швы) — 0,1 л/м² листа, только швы (Knauf); Лента разделительная по периметру — периметр стен под потолком ГКЛ; Сплошная шпаклёвка и окраска (площадь развёртки) — плоскости + борта; расход — по паспорту материала (норма расхода на сплошной слой не подтверждена); Лента LED — по оси карниза и ниши фигуры (план потолков); Требуемая мощность блоков питания — Вт/м × длина × 1,3; Установленная мощность блоков питания — сумма мощностей блоков по плану освещения; Блок питания LED — блоки потолочных лент по плану освещения (БП4, БП2, БП1, БП6, БП7); Люк ревизии — план потолков; без запаса на подрезку (при закупке листа: ×1,075 при S > 20 м², ×1,175 — 10–20 м², ×1,275 — < 10 м²).

					Проект: Дом 120 м²	М 1:50; 1:10
	Лист	№ док.	Подпись	Дата	Разрезы и узлы потолков (продолжение)	Стадия / Лист / Листов
Дизайнер	Кырлан А.С.			04.11.26		П / 47 / 136

Сечение 1.1. Короб с LED-подсветкой (М 1:10)


Пом. 1 Гостиная-кухня; карниз 150×100, щель под свет 60 мм

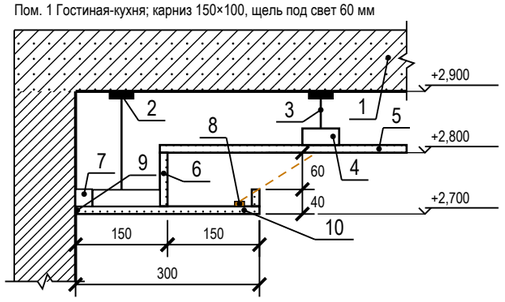

1 — плита перекрытия
2 — анкер-клин к плите — по одному на подвес
3 — подвес прямой, шаг 1000 мм
4 — ПП 60×27: несущие через 500, основные через 1200 мм; соединители одноуровневые, шурупы LN 3,5×9
5 — ГКЛ 12,5 по П113 — верхний уровень; шурупы TN 3,5×25 через 170 мм
6 — задняя стенка и бортик карниза — ГКЛ 12,5
7 — ПН 28×27 по периметру — дюбель-гвоздь через ≤ 500 мм, не менее 3 на профиль
8 — LED-лента 9,6 Вт/м, 24 В в алюминиевом профиле
9 — примыкание к стене — лента разделительная, шов зашпаклёван
10 — низ короба — ГКЛ 12,5 по ПП 60×27

Сечение 1.2. Ниша под шторы (М 1:10)


Пом. 1 Гостиная-кухня; без подсветки; закладные под карниз — до обшивки

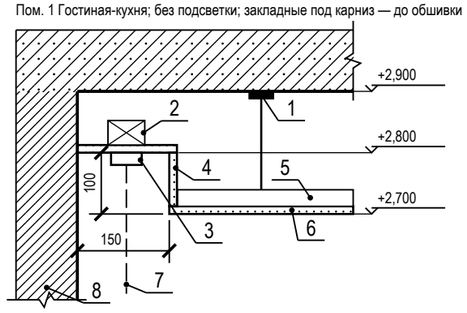

1 — анкер-клин к плите — по одному на подвес; подвес прямой, шаг 1000 мм
2 — закладная под карниз — брус 40×50
3 — карниз (шина), высота с верхом портьеры 80 мм
4 — стенка и потолок ниши — ГКЛ 12,5
5 — ПП 60×27 — каркас короба, основные через 1200 мм; соединители одноуровневые, шурупы LN 3,5×9
6 — низ короба нижнего уровня — ГКЛ 12,5; шурупы TN 3,5×25 через 170 мм
7 — портьера
8 — стена с окном

Сечение 3.1. Ниша LED фигурного уровня (М 1:10)


Пом. 3 Кабинет; карниз 120×100, щель под свет 60 мм

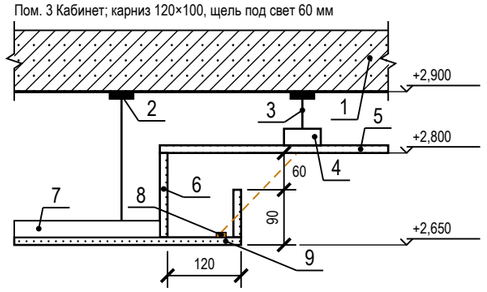

1 — плита перекрытия
2 — анкер-клин к плите — по одному на подвес
3 — подвес прямой, шаг 1000 мм
4 — ПП 60×27: несущие через 500, основные через 1200 мм; соединители одноуровневые, шурупы LN 3,5×9
5 — ГКЛ 12,5 по П113 — верхний уровень; шурупы TN 3,5×25 через 170 мм
6 — задняя стенка и бортик карниза — ГКЛ 12,5
7 — ПП 60×27 каркаса нижнего уровня, ПН по контуру фигуры (на дуге — с надрезами)
8 — LED-лента 9,6 Вт/м, 24 В в алюминиевом профиле
9 — низ короба — ГКЛ 12,5 по ПП 60×27

Сечение 3.2. Ниша под шторы (М 1:10)


Пом. 3 Кабинет; без подсветки; закладные под карниз — до обшивки

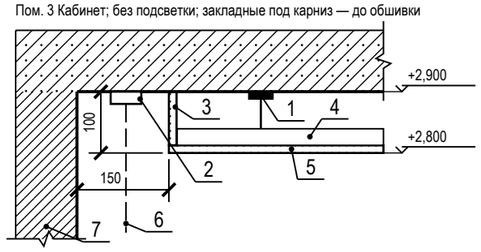

1 — анкер-клин к плите — по одному на подвес; подвес прямой, шаг 1000 мм
2 — карниз (шина), высота с верхом портьеры 80 мм
3 — стенка ниши — ГКЛ 12,5
4 — ПП 60×27 — каркас короба, основные через 1200 мм; соединители одноуровневые, шурупы LN 3,5×9
5 — низ короба нижнего уровня — ГКЛ 12,5; шурупы TN 3,5×25 через 170 мм
6 — портьера
7 — стена с окном

Сечение 3.3. Примыкание потолка к стене (М 1:10)


Пом. 3 Кабинет; примыкание — разделительная лента

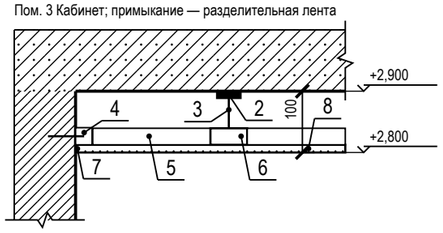

1 — плита перекрытия
2 — анкер-клин к плите — по одному на подвес
3 — подвес прямой, шаг 1000 мм
4 — ПН 28×27 по периметру — дюбель-гвоздь через ≤ 500 мм, не менее 3 на профиль
5 — ПП 60×27 несущий (вид) через 500 мм, в ПН
6 — ПП 60×27 основной (сечение) через 1200 мм; соединители одноуровневые, шурупы LN 3,5×9
7 — лента разделительная по стене, шов зашпаклёван
8 — ГКЛ 12,5 по П113; шурупы TN 3,5×25 через 170 мм

Сечение 6.1. Ниша LED фигурного уровня (М 1:10)

Пом. 6 Спальня родителей; карниз 120×100, щель под свет 60 мм

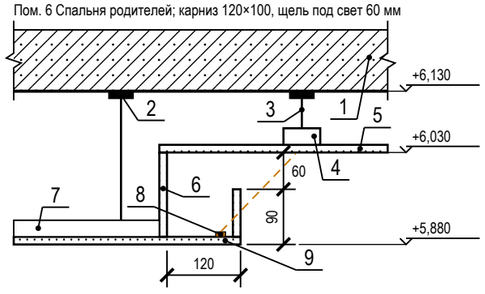

1 — плита перекрытия
2 — анкер-клин к плите — по одному на подвес
3 — подвес прямой, шаг 1000 мм
4 — ПП 60×27: несущие через 500, основные через 1200 мм; соединители одноуровневые, шурупы LN 3,5×9
5 — ГКЛ 12,5 по П113 — верхний уровень; шурупы TN 3,5×25 через 170 мм
6 — задняя стенка и бортик карниза — ГКЛ 12,5
7 — ПП 60×27 каркаса нижнего уровня, ПН по контуру фигуры (на дуге — с надрезами)
8 — LED-лента 9,6 Вт/м, 24 В в алюминиевом профиле
9 — низ короба — ГКЛ 12,5 по ПП 60×27

Условные обозначения

— · — LED-лента в нише подсветки (карниз короба, ниша фигуры)


Примечания

1. Сечения потолков М 1:10 по помещениям с нишами LED и нишами под шторы: отметки и размеры этого помещения от ±0,000 — чистого пола 1-го этажа (м, мм). Положение — по плану потолков (листы 43, 44): короб и ниша LED — по линиям ленты, ниша под шторы — у стены с окном; типовые узлы по группам помещений — на листе 45.
2. Крепёж: подвес прямой к плите на анкер-клине — по одному на подвес (Knauf П113); ПН к стенам — дюбель-гвоздь через ≤ 500 мм, не менее 3 на профиль (серия 1.045.9-2.08); лист 12,5 — шурупы TN 3,5×25 через 170 мм (СП 163, табл. 15); профили между собой — соединители одноуровневые, шурупы LN 3,5×9.
3. Изделие карниза, профиля LED и галтели подписано артикулом из данных; где артикул не выбран, сечение дано по габаритам из данных (ширина и глубина ниши, щель под свет), изделие подбирается по ним.

					Проект: Дом 120 м²	М 1:10
	Лист	№ док.	Подпись	Дата	Сечения потолков М 1:10	Стадия / Лист / Листов
Дизайнер	Кырлан А.С.			04.11.26		П / 48 / 136

Сечение 6.2. Ниша под шторы (М 1:10)

Пом. 6 Спальня родителей; без подсветки; закладные под карниз — до обшивки

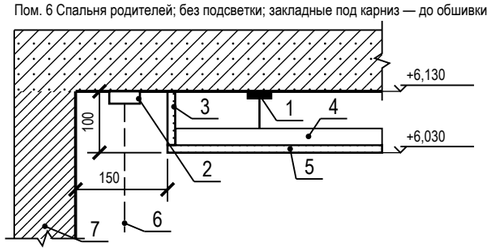

1 — анкер-клин к плите — по одному на подвес; подвес прямой, шаг 1000 мм

2 — карниз (шина), высота с верхом портьеры 80 мм

3 — стенка ниши — ГКЛ 12,5

4 — ПП 60×27 — каркас короба, основные через 1200 мм; соединители одноуровневые, шурупы LN 3,5×9


5 — низ короба нижнего уровня — ГКЛ 12,5; шурупы TN 3,5×25 через 170 мм

6 — портьера

7 — стена с окном

Сечение 6.3. Примыкание потолка к стене (М 1:10)

Пом. 6 Спальня родителей; примыкание — разделительная лента

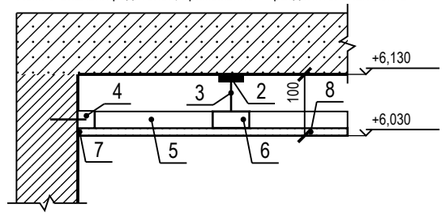

1 — плита перекрытия

2 — анкер-клин к плите — по одному на подвес

3 — подвес прямой, шаг 1000 мм

4 — ПН 28×27 по периметру — дюбель-гвоздь через ≤ 500 мм, не менее 3 на профиль

5 — ПП 60×27 несущий (вид) через 500 мм, в ПН


6 — ПП 60×27 основной (сечение) через 1200 мм; соединители одноуровневые, шурупы LN 3,5×9

7 — лента разделительная по стене, шов зашпаклёван

8 — ГКЛ 12,5 по П113; шурупы TN 3,5×25 через 170 мм

Сечение 7.1. Короб с LED-подсветкой (М 1:10)

Пом. 7 Детская, 12 Детская вторая; карниз 150×100, щель под свет 60 мм

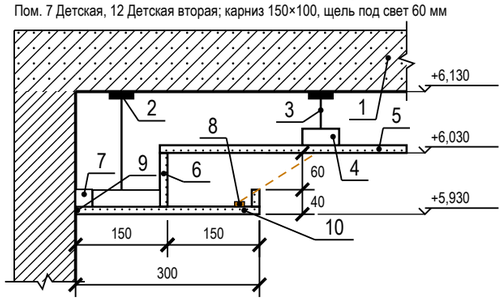

1 — плита перекрытия

2 — анкер-клин к плите — по одному на подвес

3 — подвес прямой, шаг 1000 мм

4 — ПП 60×27: несущие через 500, основные через 1200 мм; соединители одноуровневые, шурупы LN 3,5×9

5 — ГКЛ 12,5 по П113 — верхний уровень; шурупы TN 3,5×25 через 170 мм

6 — задняя стенка и бортик карниза — ГКЛ 12,5

7 — ПН 28×27 по периметру — дюбель-гвоздь через ≤ 500 мм, не менее 3 на профиль


8 — LED-лента 9,6 Вт/м, 24 В в алюминиевом профиле

9 — примыкание к стене — лента разделительная, шов зашпаклёван

10 — низ короба — ГКЛ 12,5 по ПП 60×27

Сечение 7.2. Ниша под шторы (М 1:10)

Пом. 7 Детская, 12 Детская вторая; без подсветки; закладные под карниз — до обшивки

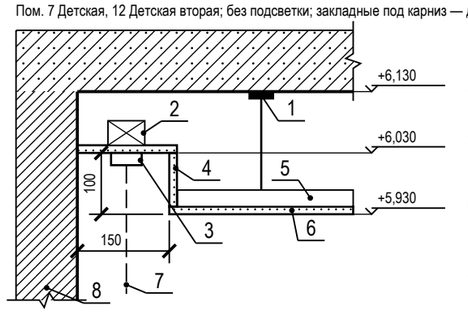

1 — анкер-клин к плите — по одному на подвес; подвес прямой, шаг 1000 мм

2 — закладная под карниз — брус 40×50

3 — карниз (шина), высота с верхом портьеры 80 мм

4 — стенка и потолок ниши — ГКЛ 12,5

5 — ПП 60×27 — каркас короба, основные через 1200 мм; соединители одноуровневые, шурупы LN 3,5×9

6 — низ короба нижнего уровня — ГКЛ 12,5; шурупы TN 3,5×25 через 170 мм

7 — портьера

8 — стена с окном

Условные обозначения

— · — · LED-лента в нише подсветки (карниз короба, ниша фигуры)

Примечания

1. Сечения потолков М 1:10 по помещениям с нишами LED и нишами под шторы: отметки и размеры этого помещения от ±0,000 — чистого пола 1-го этажа (м, мм). Положение — по плану потолков (листы 43, 44): короб и ниша LED — по линиям ленты, ниша под шторы — у стены с окном; типовые узлы по группам помещений — на листе 45.
2. Крепёж: подвес прямой к плите на анкер-клине — по одному на подвес (Knauf П113); ПН к стенам — дюбель-гвоздь через ≤ 500 мм, не менее 3 на профиль (серия 1.045.9-2.08); лист 12,5 — шурупы TN 3,5×25 через 170 мм (СП 163, табл. 15); профили между собой — соединители одноуровневые, шурупы LN 3,5×9.
3. Изделие карниза, профиля LED и галтели подписано артикулом из данных; где артикул не выбран, сечение дано по габаритам из данных (ширина и глубина ниши, щель под свет), изделие подбирается по ним.

					Проект: Дом 120 м²	**М 1:10**
	Лист	№ док.	Подпись	Дата	Сечения потолков М 1:10	Стадия / Лист / Листов
Дизайнер	Кырлан А.С.			04.11.26		П / 49 / 136

Условные обозначения

Данные щитка

Показатель	Значение
Номер щитка	ЩК
Тип	ЩРВ-П-54, IP41
Уст. мощность, кВт	30,4
Разреш. мощность, кВт	15
Расчётная, кВт	12,6
Автоматы 1п: занят. / рез.	17 / 4
Модулей: всего / занято	54 / 40
Ток на вводе, А	63
Вводной аппарат	QF0 C63, 2P
УЗИП	FV1, тип 2, ЩК, после счётчика
ГЗШ, проводник ОСУП	Cu 6 мм²
Листов схемы	2 (группы по листам)

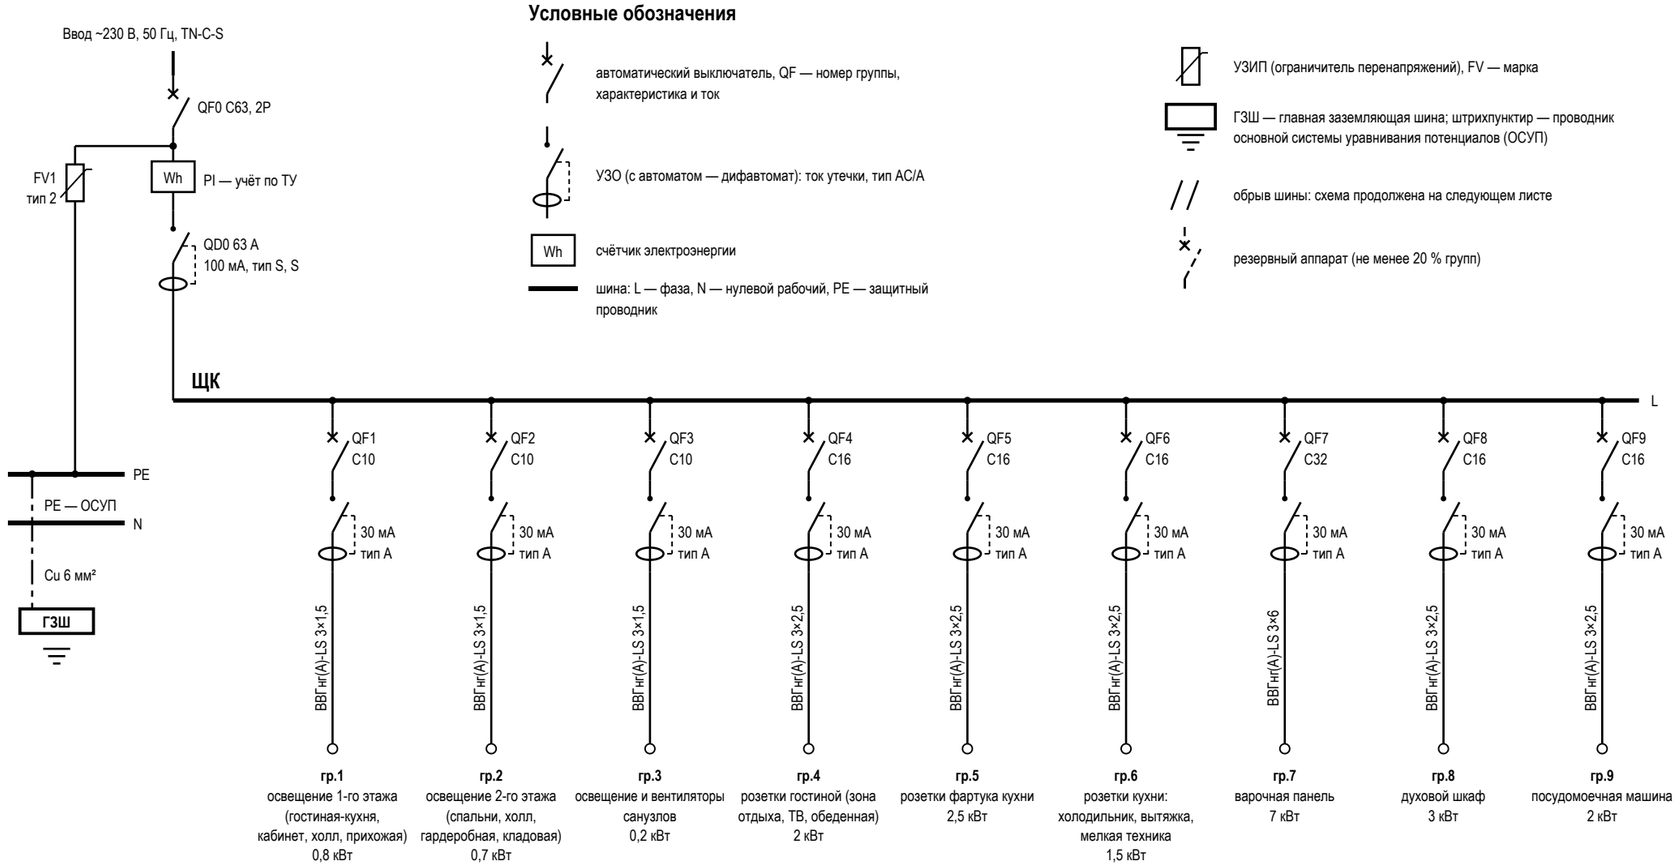


Таблица групп щита ЩК и кабельный журнал

№	Назначение	Помещения	Автомат	УЗО / дифавтомат	Кабель	Длина, м	P, кВт	Точек
1	освещение 1-го этажа (гостиная-кухня, кабинет, холл, прихожая)	2, 3, 5, 6, 7, 8, 9, 10, 12	C10	30 мА, тип A	ВВГнг(A)-LS 3×1,5	200,9	0,8	53
2	освещение 2-го этажа (спальни, холл, гардеробная, кладовая)	1, 2, 5, 10, 11	C10	30 мА, тип A	ВВГнг(A)-LS 3×1,5	119,3	0,7	42
3	освещение и вентиляторы санузлов	4, 11, 13	C10	30 мА, тип A	ВВГнг(A)-LS 3×1,5	50,6	0,2	11
4	розетки гостиной (зона отдыха, ТВ, обеденная)	6	C16	30 мА, тип A	ВВГнг(A)-LS 3×2,5	37,8	2	6
5	розетки фартука кухни	3, 7, 12	C16	30 мА, тип A	ВВГнг(A)-LS 3×2,5	76,1	2,5	13
6	розетки кухни: холодильник, вытяжка, мелкая техника	1, 2, 5, 10	C16	30 мА, тип A	ВВГнг(A)-LS 3×2,5	60,7	1,5	11
7	варочная панель	1	C32	30 мА, тип A	ВВГнг(A)-LS 3×6	29,8	7	6
8	духовой шкаф	1	C16	30 мА, тип A	ВВГнг(A)-LS 3×2,5	13,9	3	1
9	посудомоечная машина	1	C16	30 мА, тип A	ВВГнг(A)-LS 3×2,5	12,1	2	1

Примечания

1. Схема однолинейная: одна линия — фаза, N и PE группы; аппараты — в отключённом положении (ГОСТ 2.702, ГОСТ 2.755). Номера групп — как у точек на планах (гр.). За отметку 0,000 принят уровень чистого пола; высота щита — по плану розеток.
2. Розеточные и мокрые линии — через УЗО или дифавтомат с током утечки не более 30 мА (ПУЭ 7.1.79); в санузле выполнить ДСУП (ПУЭ 7.1.87–7.1.88).
3. УЗО тип A — для линий с электроникой, стиральной и посудомоечной машиной, LED-драйверами; тип AC — только для чисто активной нагрузки.
4. Кабель — медный, исполнение нг(A)-LS (ГОСТ 31565-2012); скрытая прокладка только горизонтально и вертикально, фактические трассы зафиксировать исполнительной схемой до закрытия отделкой.
5. Номинал автомата — не выше допустимого тока кабеля: 1,5 мм² — до 10 А, 2,5 мм² — до 16 А. Резерв щита — не менее 20 % модулей.
6. Расчёт нагрузок, токов КЗ, селективности и сечений — по проекту ЭОМ организации с допуском СРО; лист задаёт состав, расположение и группы.
7. УЗИП FV1 — после вводного автомата, проводник к шине PE — кратчайший, без петель. Шина PE щита соединяется с ГЗШ проводником ОСУП; к ГЗШ присоединяются трубы водопровода и отопления на вводе в квартиру (ПУЭ 7.1.87). Шины N и PE — раздельные, после разделения PEN не объединяются.
8. До подключения нагрузки — приёмо-сдаточные испытания с протоколом: сопротивление изоляции линий не менее 0,5 МОм, срабатывание УЗО по току и времени, непрерывность защитных проводников PE (ПУЭ, гл. 1.8).

					Проект: Дом 120 м²
	Лист	№ док.	Подпись	Дата	Однолинейная схема щита
Дизайнер	Кырлан А.С.			04.11.26	

Стадия	Лист	Листов
П	50	136

Продолжение однолинейной схемы щита ЩК, начало — лист 50

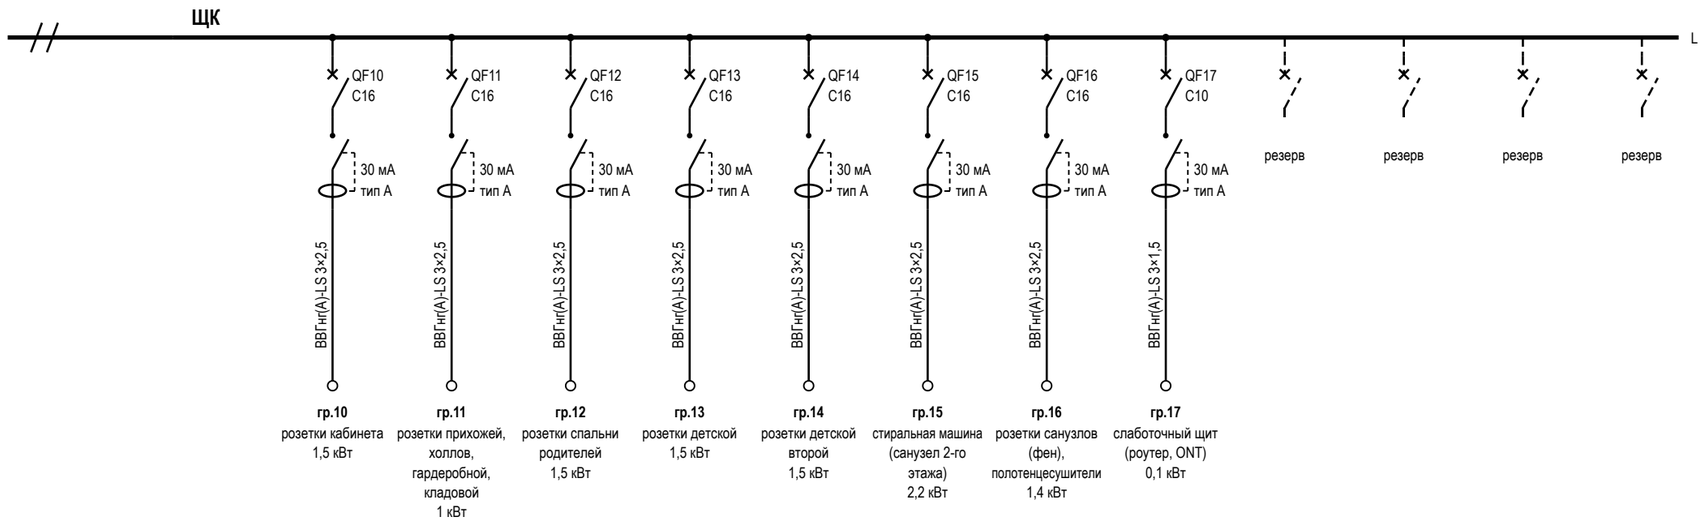


Таблица групп щита ЩК и кабельный журнал (продолжение)


№	Назначение	Помещения	Автомат	УЗО / дифавтомат	Кабель	Длина, м	Р, кВт	Точек
10	розетки кабинета	1	C16	30 мА, тип A	ВВГнг(A)-LS 3×2,5	15,3	1,5	1
11	розетки прихожей, холлов, гардеробной, кладовой	1, 11	C16	30 мА, тип A	ВВГнг(A)-LS 3×2,5	20,9	1	3
12	розетки спальни родителей		C16	30 мА, тип A	ВВГнг(A)-LS 3×2,5	13,8	1,5	0
13	розетки детской		C16	30 мА, тип A	ВВГнг(A)-LS 3×2,5	27,4	1,5	0
14	розетки детской второй		C16	30 мА, тип A	ВВГнг(A)-LS 3×2,5	4,1	1,5	0
15	стиральная машина (санузел 2-го этажа)	13	C16	30 мА, тип A	ВВГнг(A)-LS 3×2,5	20	2,2	1
16	розетки санузлов (фен), полотенцесушители	4, 13	C16	30 мА, тип A	ВВГнг(A)-LS 3×2,5	35	1,4	3
17	слаботочный щит (роутер, ONT)	5	C10	30 мА, тип A	ВВГнг(A)-LS 3×1,5	5	0,1	1
	Итого по сечениям ВВГнг(A)-LS (все группы щита), м: 3×1,5 — 375,8; 3×2,5 — 337,1; 3×6 — 29,8					742,7		

Примечания

1. Лист — продолжение однолинейной схемы щита ЩК: начало, данные щитка и условные обозначения — лист 50. Ввод, учёт, вводной аппарат, УЗИП, шины N и PE и ГЗШ показаны там же; шина L листа — та же шина щита.
2. Схема однолинейная: одна линия — фаза, N и PE группы; аппараты — в отключённом положении (ГОСТ 2.702, ГОСТ 2.755). Номера групп — как у точек на планах (гр.). За отметку 0,000 принят уровень чистого пола; высота щита — по плану розеток.
3. Розеточные и мокрые линии — через УЗО или дифавтомат с током утечки не более 30 мА (ПУЭ 7.1.79); в санузле выполнить ДСУП (ПУЭ 7.1.87–7.1.88).
4. УЗО тип A — для линий с электроникой, стиральной и посудомоечной машиной, LED-драйверами; тип AC — только для чисто активной нагрузки.
5. Кабель — медный, исполнение нг(A)-LS (ГОСТ 31565-2012); скрытая прокладка только горизонтально и вертикально, фактические трассы зафиксировать исполнительной схемой до закрытия отделкой.
6. Номинал автомата — не выше допустимого тока кабеля: 1,5 мм² — до 10 А, 2,5 мм² — до 16 А. Резерв щита — не менее 20 % модулей.
7. Расчёт нагрузок, токов КЗ, селективности и сечений — по проекту ЭОМ организации с допуском СРО; лист задаёт состав, расположение и группы.
8. До подключения нагрузки — приёмо-сдаточные испытания с протоколом: сопротивление изоляции линий не менее 0,5 МОм, срабатывание УЗО по току и времени, непрерывность защитных проводников PE (ПУЭ, гл. 1.8).

					Проект: Дом 120 м²
	Лист	№ док.	Подпись	Дата	Однолинейная схема щита (продолжение)
Дизайнер	Кырлан А.С.			04.11.26	

Стадия	Лист	Листов
П	51	136

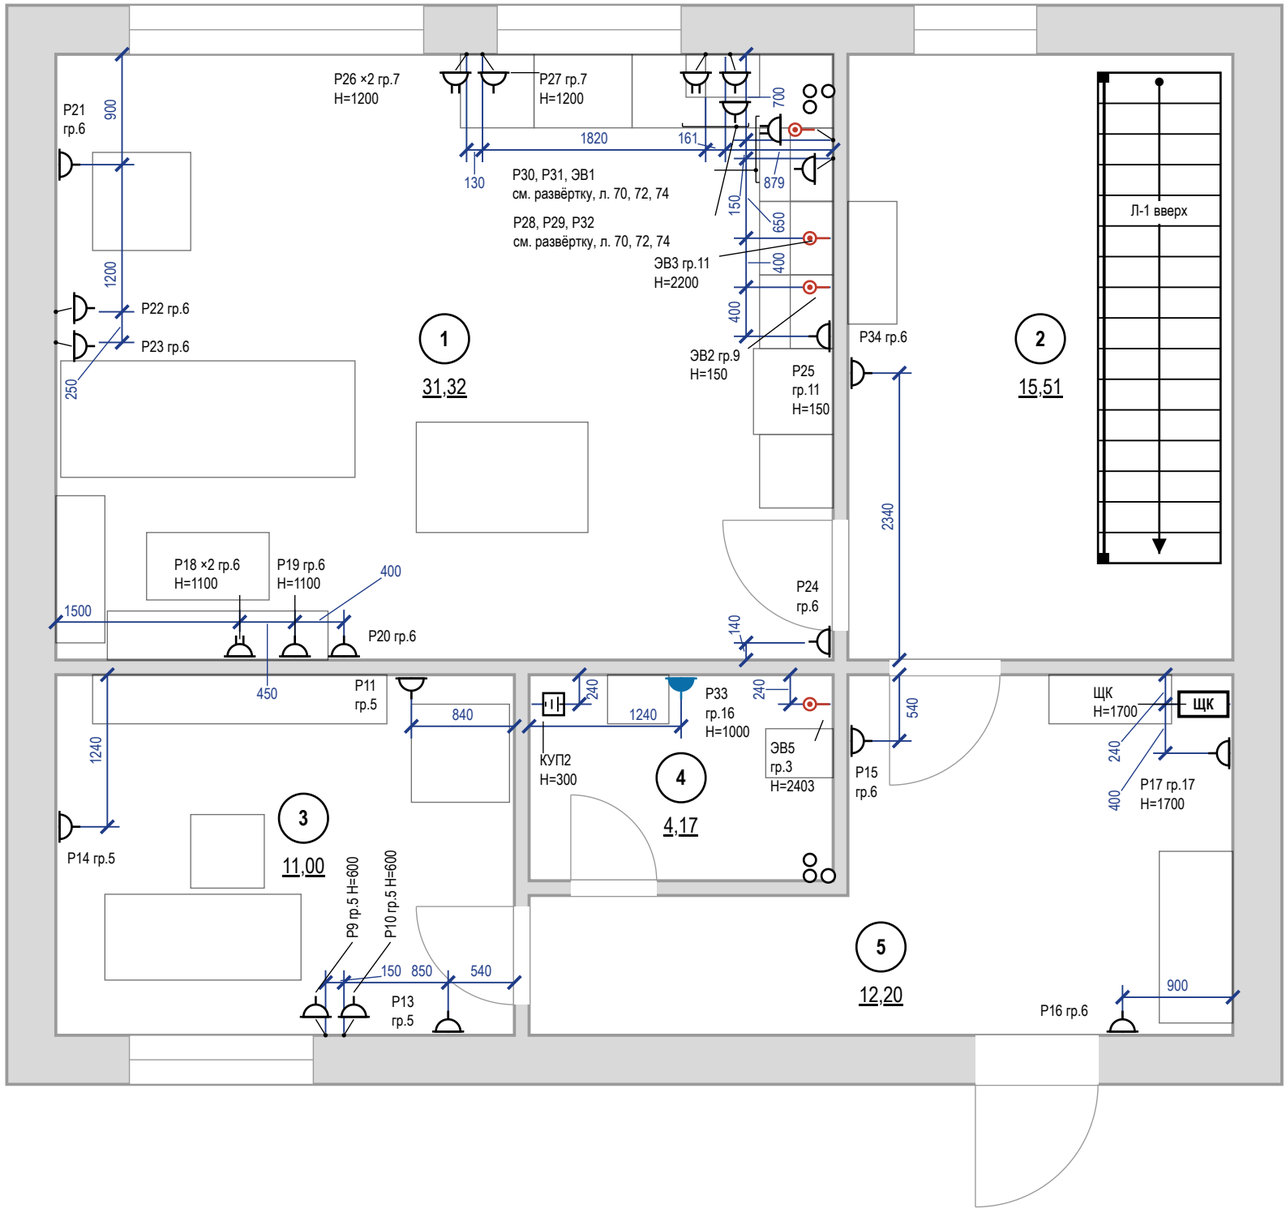

Условные обозначения

Знак	Тип изделия	H, мм	Кол., шт
	Розетка с заземлением	300	12
	То же	у знака	8
	Блок розеток с заземлением, рамка 2 поста	у знака	4
	Розетка с заземлением IP44	1000	1
	Вывод кабеля к прибору	у знака	4
	КУП (уравнивание потенциалов)	300	1
ЩК	Щит квартирный	1700	1

розетка с заземляющим контактом; у знака — марка, ×N — постов в рамке, гр. — группа щита, H — высота оси, мм

знак разведён для читаемости: точка на стене — у выноски, привязка — до неё

мебель и сантехприборы — подложка

стояк: К1 — канализация, В1 — ХВС, Т3 — ГВС


1 — номер помещения, площадь м²

Итого розеток (механизмов) — 29 шт; рамок — 25 шт: на 1 пост — 21, на 2 поста — 4.

Примечания

1. За отметку 0,000 принят уровень чистого пола. Высоты H — от чистого пола до оси изделия; привязки — от чистовой грани стены до оси механизма (у рамки на несколько постов — до оси рамки).
2. Розетки без отметки H у знака — на высоте 300 мм от чистого пола до оси механизма; выводы кабеля — по паспорту прибора.
3. Розетки в санузле — только вне зон 0–2 (ПУЭ 7.1.48, ГОСТ Р 50571.7.701-2024), IP44, через УЗО 30 мА.
4. Розеточные и мокрые линии — через УЗО или дифавтомат с током утечки не более 30 мА (ПУЭ 7.1.79); в санузле выполнить ДСУП (ПУЭ 7.1.87–7.1.88).
5. Кабель — медный, исполнение нг(A)-LS (ГОСТ 31565-2012); скрытая прокладка только горизонтально и вертикально, фактические трассы зафиксировать исполнительной схемой до закрытия отделкой.
6. Расчёт нагрузок, токов КЗ, селективности и сечений — по проекту ЭОМ организации с допуском СРО; лист задаёт состав, расположение и группы.
7. Выводы кухонной техники — после утверждения проекта кухни (ориентировочно); привязки выводов даны от осей модулей гарнитура и пересматриваются вместе с проектом кухни.
8. Электрический тёплый пол проектом не предусмотрен; при решении заказчика устроить — отдельный лист «План тёплых полов»: контуры с отступом 100 мм от стен и мебели без ножек, датчик в гофре, терморегулятор, своя группа щита через УЗО 30 мА.

					Проект: Дом 120 м²			M 1:50
	Лист	№ док.	Подпись	Дата	План розеток и электровыводов · 1-й этаж	Стадия	Лист	Листов
Дизайнер	Кырлан А.С.			04.11.26		П	52	136

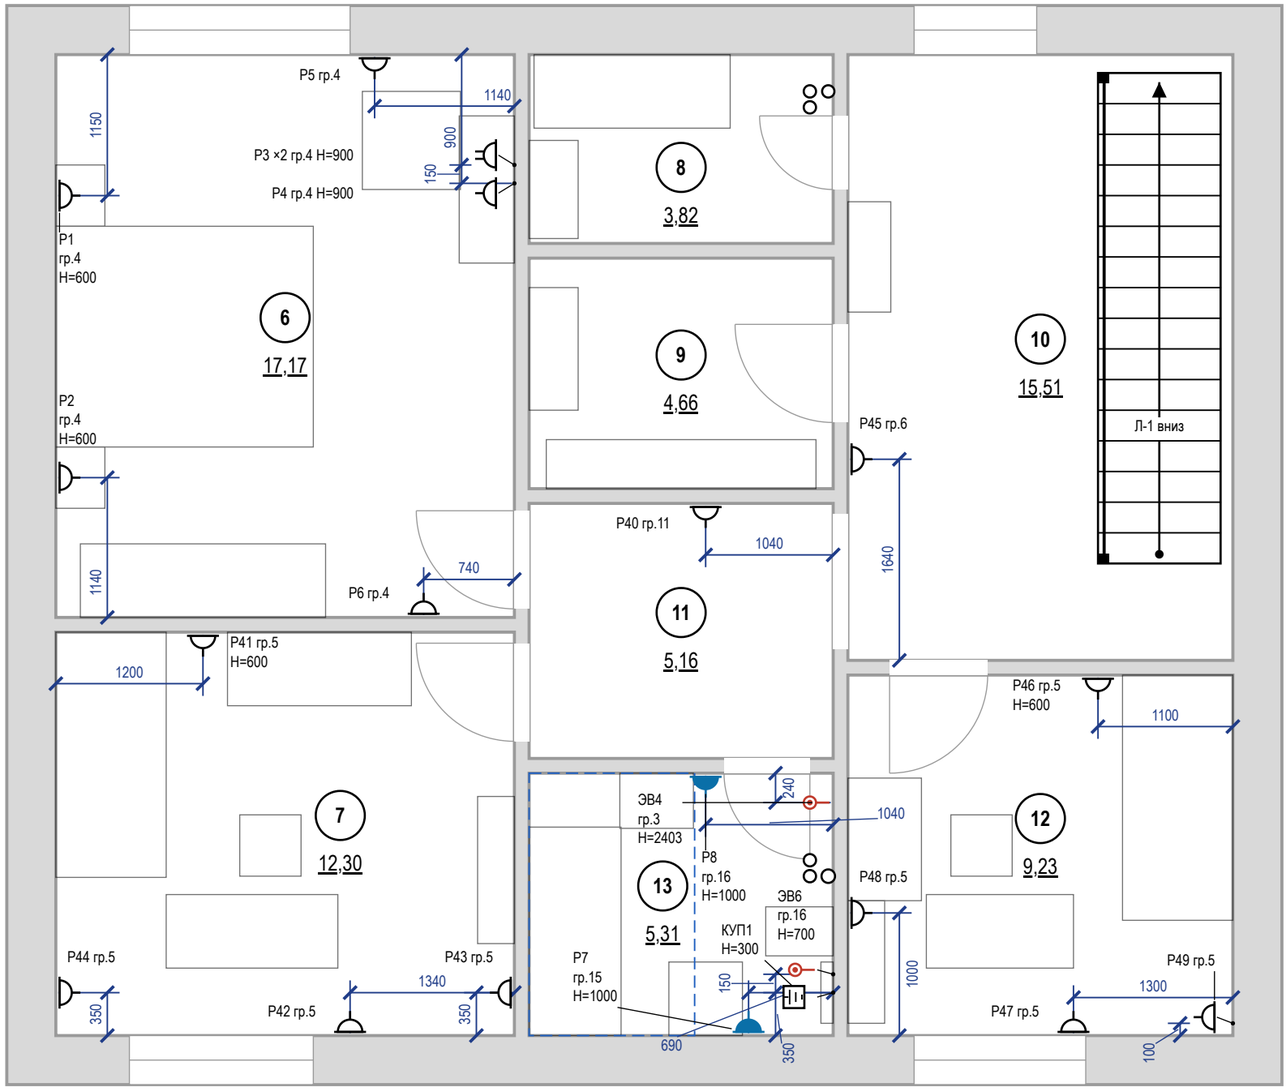

Условные обозначения

Знак	Тип изделия	Н, мм	Кол., шт
	Розетка с заземлением	300	10
	То же	у знака	5
	Блок розеток с заземлением, рамка 2 поста	900	1
	Розетка с заземлением IP44	1000	2
	Вывод кабеля к прибору	у знака	2
	КУП (уравнивание потенциалов)	300	1

розетка с заземляющим контактом; у знака — марка, ×N — постов в рамке, гр. — группа щита, Н — высота оси, мм

знак разведён для читаемости: точка на стене — у выноски, привязка — до неё

граница зоны 2 ванной (600 мм от ванны/поддона)

мебель и сантехприборы — подложка

стояк: К1 — канализация, В1 — ХВС, Т3 — ГВС


1 — номер помещения, площадь м²

Итого розеток (механизмов) — 19 шт; рамок — 18 шт: на 1 пост — 17, на 2 поста — 1.

Примечания

1. За отметку 0,000 принят уровень чистого пола. Высоты Н — от чистого пола до оси изделия; привязки — от чистовой грани стены до оси механизма (у рамки на несколько постов — до оси рамки).
2. Розетки без отметки Н у знака — на высоте 300 мм от чистого пола до оси механизма; выводы кабеля — по паспорту прибора.
3. Розетки в санузле — только вне зон 0–2 (ПУЭ 7.1.48, ГОСТ Р 50571.7.701-2024), IP44, через УЗО 30 мА.
4. Розеточные и мокрые линии — через УЗО или дифавтомат с током утечки не более 30 мА (ПУЭ 7.1.79); в санузле выполнить ДСУП (ПУЭ 7.1.87–7.1.88).
5. Кабель — медный, исполнение нг(А)-LS (ГОСТ 31565-2012); скрытая прокладка только горизонтально и вертикально, фактические трассы зафиксировать исполнительной схемой до закрытия отделкой.
6. Расчёт нагрузок, токов КЗ, селективности и сечений — по проекту ЭОМ организации с допуском СРО; лист задаёт состав, расположение и группы.
7. Электрический тёплый пол проектом не предусмотрен; при решении заказчика устроить — отдельный лист «План тёплых полов»: контуры с отступом 100 мм от стен и мебели без ножек, датчик в гофре, терморегулятор, своя группа щита через УЗО 30 мА.

					Проект: Дом 120 м² — М 1:50
	Лист	№ док.	Подпись	Дата	
Дизайнер	Кырлан А.С.			04.11.26	План розеток и электровыводов · 2-й этаж
					Стадия: П; Лист: 53; Листов: 136

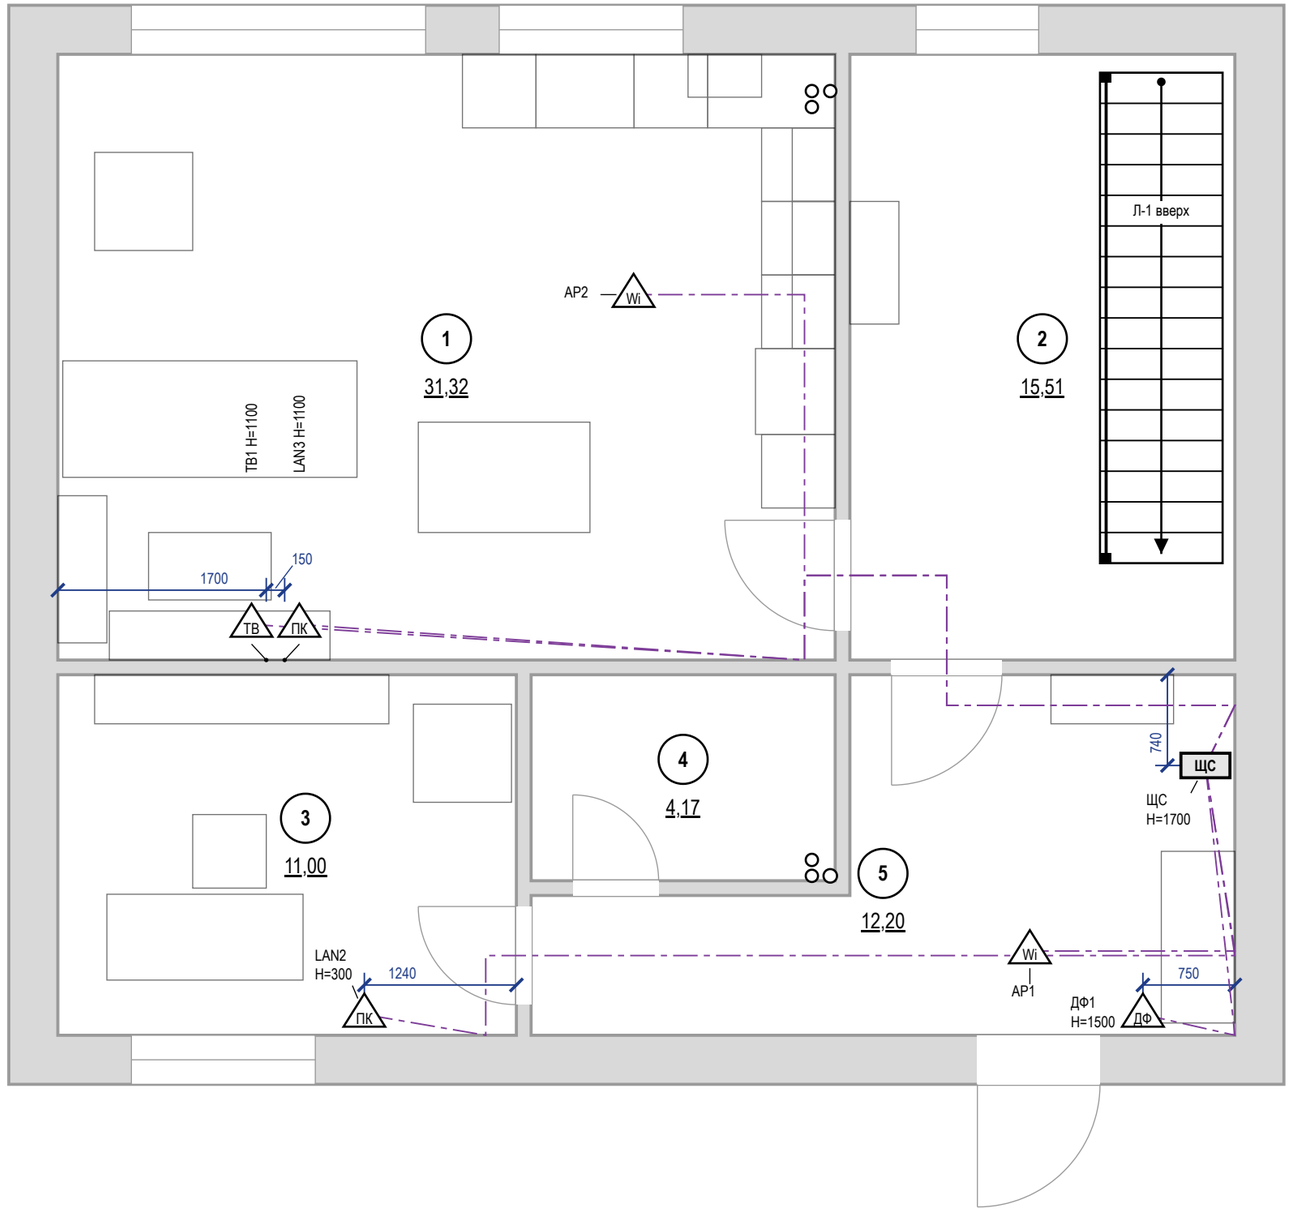

Условные обозначения

- **ЩС** — щит слаботочный: ввод провайдера, роутер, коммутатор
- **ПК** — розетка компьютерная RJ45
- **ТВ** — розетка телевизионная
- **ДФ** — трубка или монитор домофона
- **Wi** — точка доступа Wi-Fi (питание PoE)
- кабель от ЩС до точки, отдельным лучом
- мебель и сантехприборы подложка
- стояк: К1 канализация, В1 ХВС, Т3 — ГВС
- **1** — номер помещения, площадь м²

Примечания


1. За отметку 0,000 принят уровень чистого пола. Высоты Н — от чистого пола до оси изделия; привязки — от чистовой грани стены до оси механизма (у рамки на несколько постов — до оси рамки).
2. Высота установки, не указанная на плане: розетки LAN и ТВ — 300 мм от чистого пола.
3. Слаботочные кабели — отдельно от силовых: в своей трубе или лотке, при параллельной прокладке не ближе 100 мм к силовым, пересечения под прямым углом; каждую точку — отдельным кабелем от ЩС без скруток.
4. Трассы на листе — принципиальные; фактические зафиксировать исполнительной схемой до закрытия отделкой. Силовые линии, УЗО 30 мА, ДСУП, кабель нг(А)-LS — по листам розеток и щита.
5. Проект силовой части и расчёт токов КЗ — по проекту ЭОМ; слаботочная часть согласуется с провайдером (ввод в дом, место ONT) и с заказчиком (вызывная панель у калитки, антенна или спутниковое ТВ).

	Лист	№ док.	Подпись	Дата
Дизайнер	Кырлан А.С.			04.11.26

Проект: Дом 120 м² — **М 1:50**

План слаботочных сетей · 1-й этаж

Стадия	Лист	Листов
П	54	136

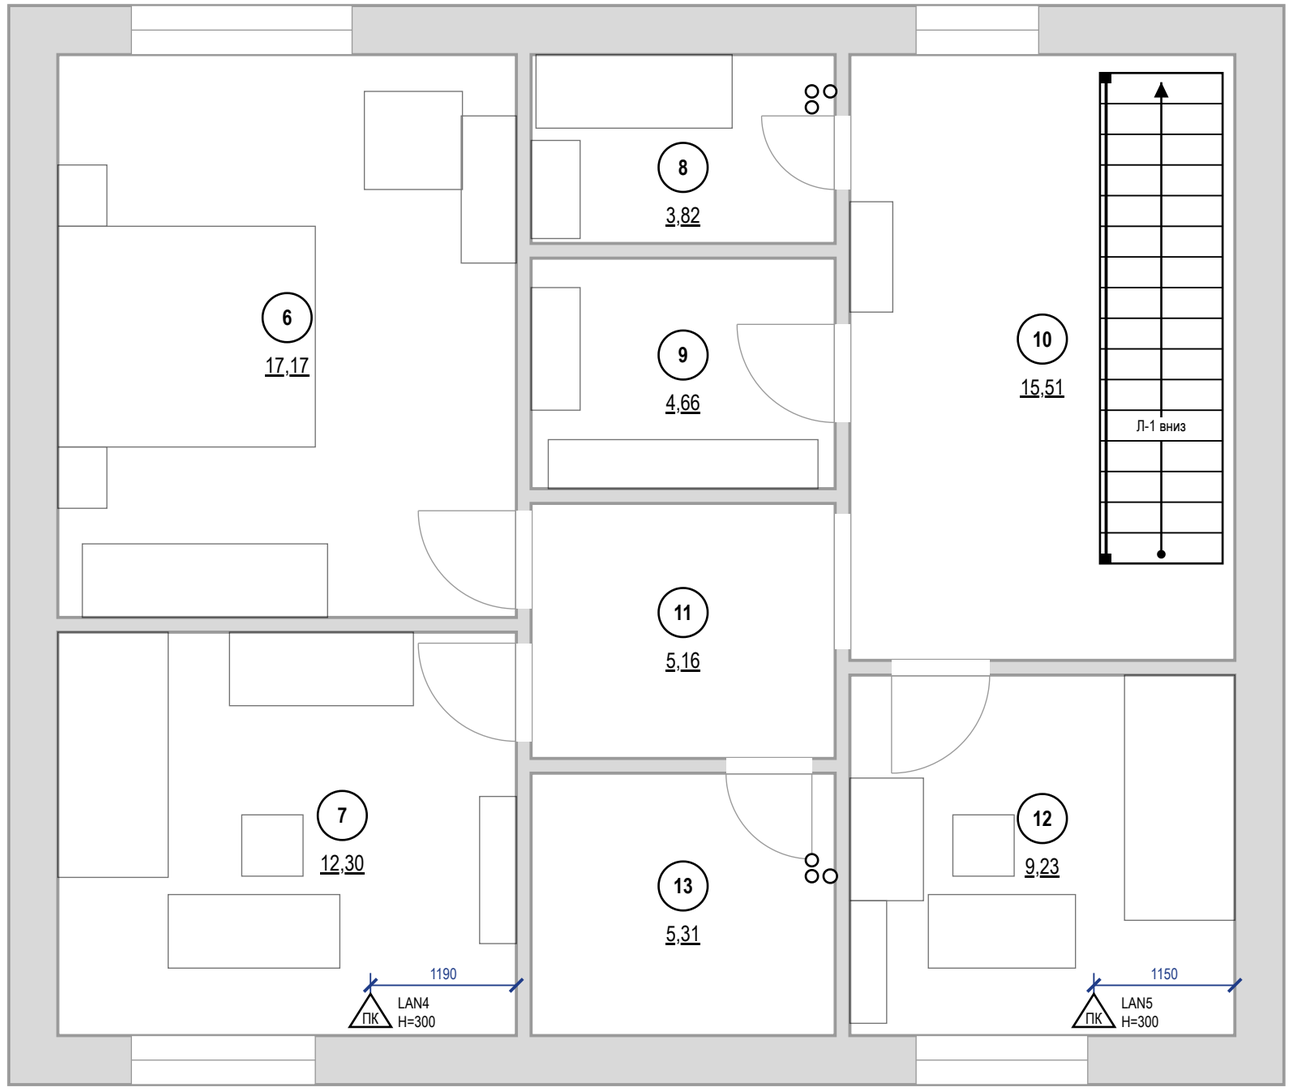

Примечания

1. За отметку 0,000 принят уровень чистого пола. Высоты H — от чистого пола до оси изделия; привязки — от чистовой грани стены до оси механизма (у рамки на несколько постов — до оси рамки).
2. Высота установки, не указанная на плане: розетки LAN и ТВ — 300 мм от чистого пола.
3. Слаботочные кабели — отдельно от силовых: в своей трубе или лотке, при параллельной прокладке не ближе 100 мм к силовым, пересечения под прямым углом; каждую точку — отдельным кабелем от ЩС без скруток.
4. Трассы на листе — принципиальные; фактические зафиксировать исполнительной схемой до закрытия отделкой. Силовые линии, УЗО 30 мА, ДСУП, кабель нг(A)-LS — по листам розеток и щита.
5. Проект силовой части и расчёт токов КЗ — по проекту ЭОМ; слаботочная часть согласуется с провайдером (ввод в дом, место ONT) и с заказчиком (вызывная панель у калитки, антенна или спутниковое ТВ).

Условные обозначения

ПК — розетка компьютерная RJ45

мебель и сантехприборы — подложка

стояк: К1 — канализация, В1 — ХВС, Т3 — ГВС


1 — номер помещения, площадь м²

	Лист	№ док.	Подпись	Дата
Дизайнер	Кырлан А.С.			04.11.26

Проект: Дом 120 м² — **М 1:50**

План слаботочных сетей · 2-й этаж

Стадия	Лист	Листов
П	55	136

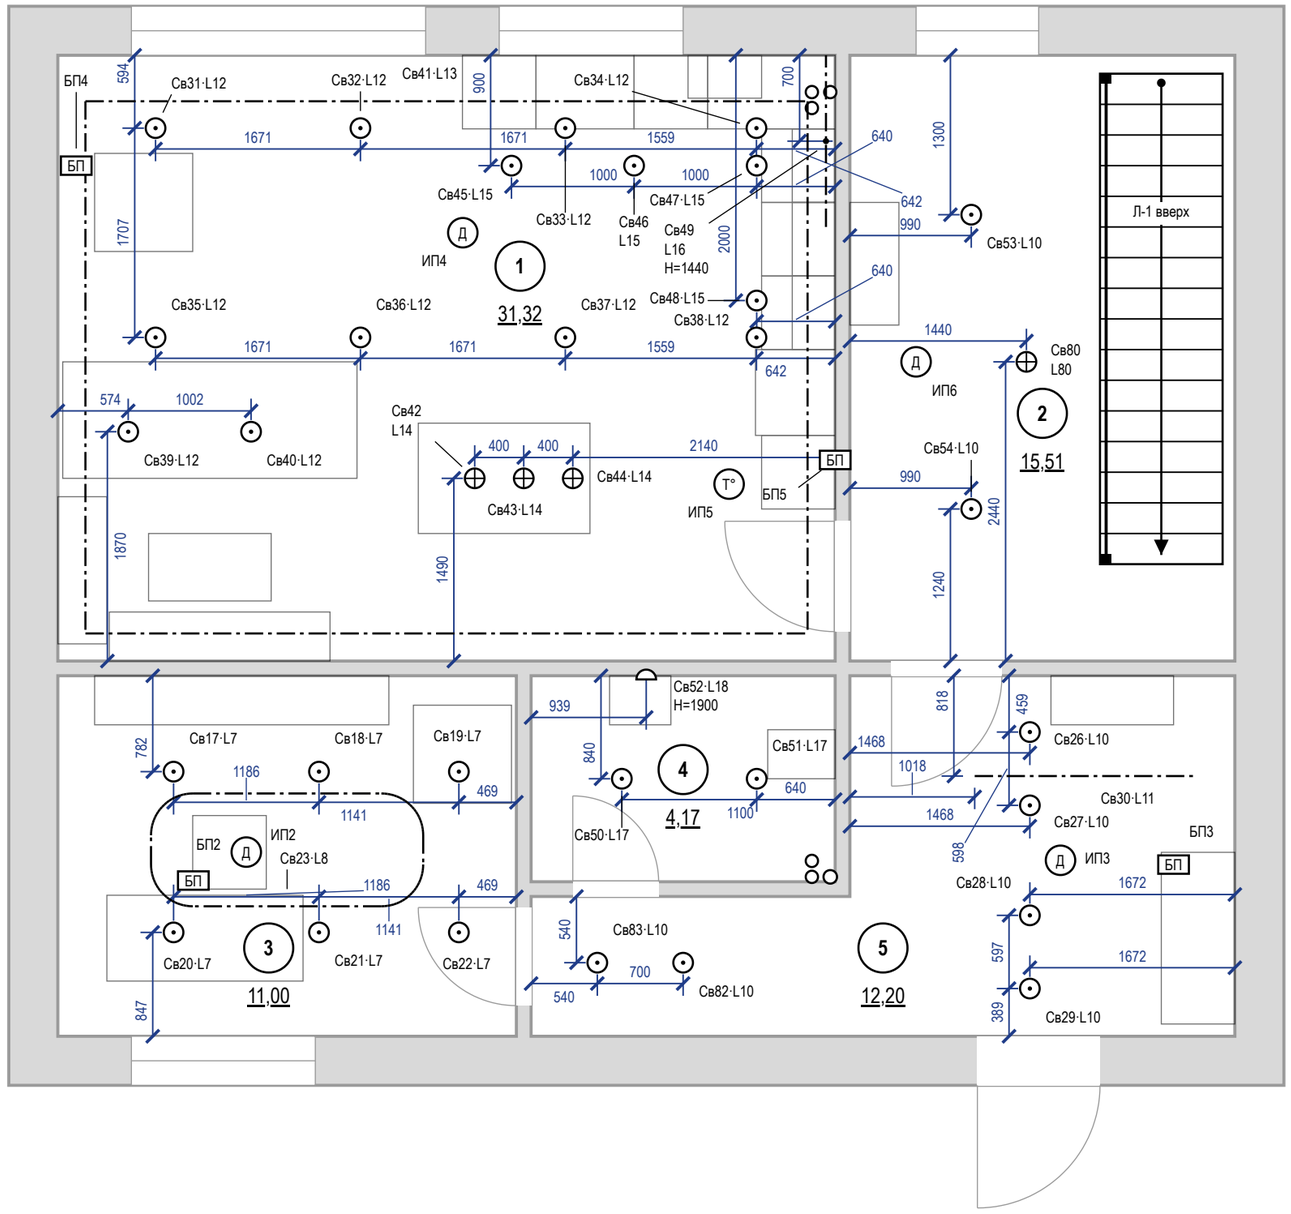

Условные обозначения

⊙	светильник встраиваемый точечный	Д	извещатель пожарный дымовой автономный
⊕	светильник подвесной	T°	извещатель пожарный тепловой
⊃	светильник настенный (бра), H — высота оси	БП	блок питания LED, с доступом (люк от 100×100 мм)
—•—	линейный светильник настенный (подсветка столешницы), точка вывод питания	▭	мебель и сантехприборы подложка
— · —	светодиодная лента в профиле / в карнизе короба	○	стояк: К1 канализация, В1 ХВС, Т3 — ГВС
Св1·L1	марка светильника (как в ведомости и на развёртках) · группа включения L (лист 59)	1	номер помещения, площадь м²

Примечания


1. За отметку 0,000 принят уровень чистого пола. Высоты H — от чистого пола до оси изделия; привязки — от чистовой грани стены до оси механизма (у рамки на несколько постов — до оси рамки).
2. Высота установки, не указанная на плане: светильники — на потолке; настенные — по отметке H у знака. Привязки — до оси светильника от чистовой грани стены, по рядам.
3. Во влажных помещениях — светильники не ниже IP44; в зонах 0–2 ванной — по ГОСТ Р 50571.7.701-2024 (зона 1 — IPX5).
4. LED-лента в карнизе подсветки короба — по линии карниза с плана потолков; блок питания — в люке короба (БП на плане), питание ленты длиннее 5 м — с двух концов.
5. Розеточные и мокрые линии — через УЗО или дифавтомат с током утечки не более 30 мА (ПУЭ 7.1.79); в санузле выполнить ДСУП (ПУЭ 7.1.87–7.1.88).
6. Кабель — медный, исполнение нг(A)-LS (ГОСТ 31565-2012); скрытая прокладка только горизонтально и вертикально, фактические трассы зафиксировать исполнительной схемой до закрытия отделкой.
7. Расчёт нагрузок, токов КЗ, селективности и сечений — по проекту ЭОМ организации с допуском СРО; лист задаёт состав, расположение и группы.
8. Ведомость светильников (тип, количество, мощность, поток, Tц, Ra) — лист 58.

	Лист	№ док.	Подпись	Дата
Дизайнер	Кырлан А.С.			04.11.26

Проект: Дом 120 м² — **М 1:50**

План освещения · 1-й этаж

Стадия	Лист	Листов
П	56	136

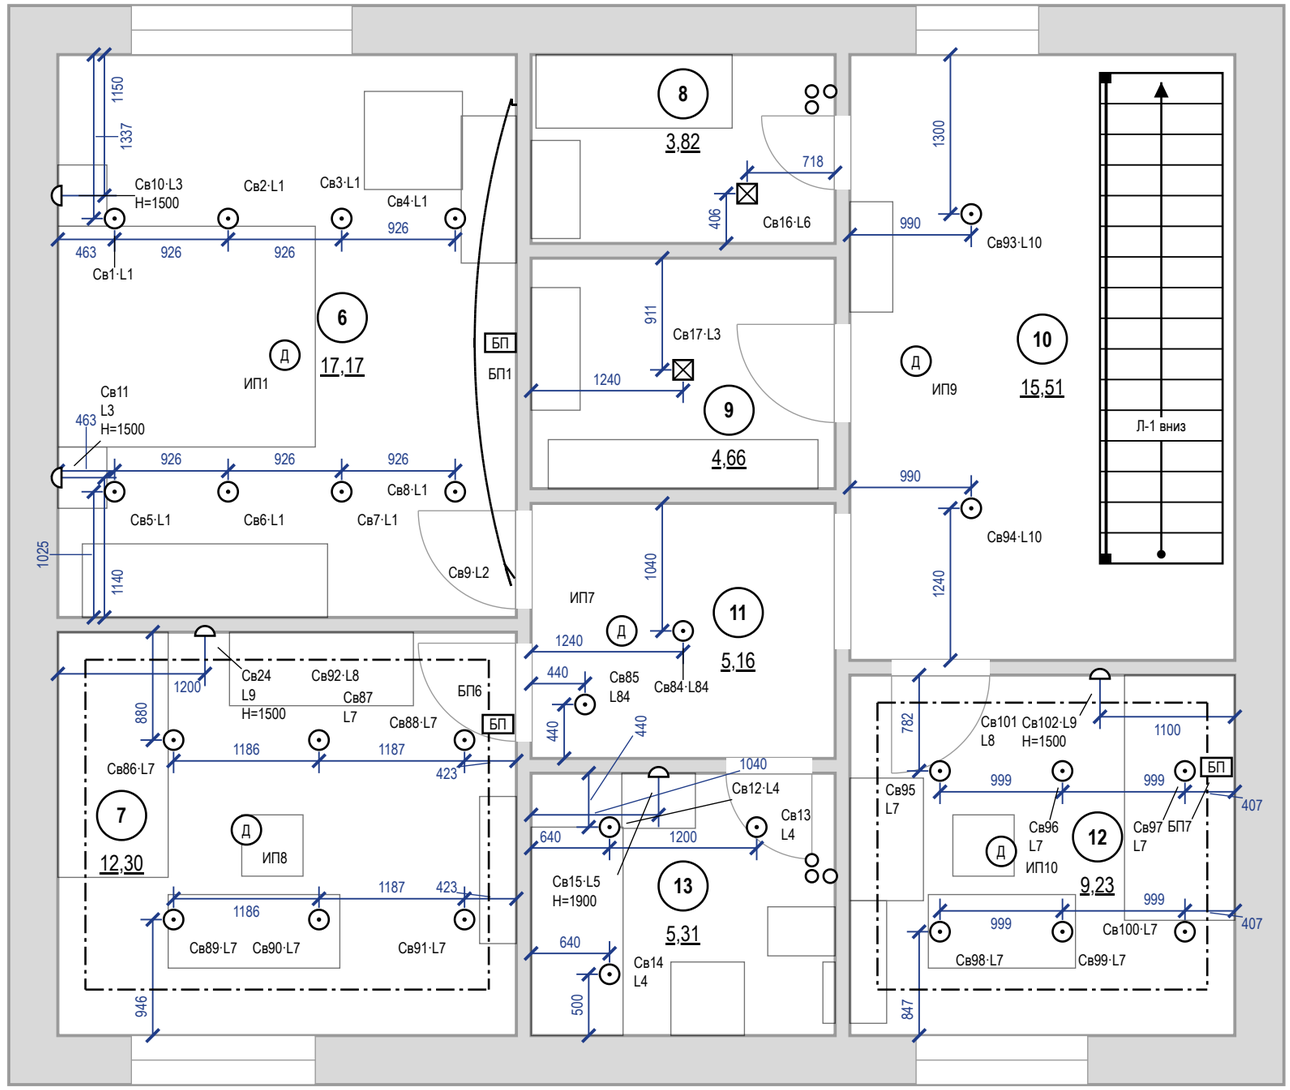

Условные обозначения

- светильник встраиваемый точечный
- светильник потолочный накладной
- светильник настенный (бра), H — высота оси
- светодиодная лента в профиле / в карнизе короба
- Св1·L1 — марка светильника (как в ведомости и на развёртках) · группа включения L (лист 59)
- Д — извещатель пожарный дымовой автономный
- БП — блок питания LED, с доступом (люк от 100×100 мм)
- мебель и сантехприборы подложка
- стояк: К1 канализация, В1 ХВС, Т3 — ГВС
- 1 — номер помещения, площадь м²

Примечания

1. За отметку 0,000 принят уровень чистого пола. Высоты H — от чистого пола до оси изделия; привязки — от чистовой грани стены до оси механизма (у рамки на несколько постов — до оси рамки).
2. Высота установки, не указанная на плане: светильники — на потолке; настенные — по отметке H у знака. Привязки — до оси светильника от чистовой грани стены, по рядам.
3. Во влажных помещениях — светильники не ниже IP44; в зонах 0–2 ванной — по ГОСТ Р 50571.7.701-2024 (зона 1 — IPX5).
4. LED-лента в карнизе подсветки короба — по линии карниза с плана потолков; блок питания — в люке короба (БП на плане), питание ленты длиннее 5 м — с двух концов.
5. Розеточные и мокрые линии — через УЗО или дифавтомат с током утечки не более 30 мА (ПУЭ 7.1.79); в санузле выполнить ДСУП (ПУЭ 7.1.87–7.1.88).
6. Кабель — медный, исполнение нг(A)-LS (ГОСТ 31565-2012); скрытая прокладка только горизонтально и вертикально, фактические трассы зафиксировать исполнительной схемой до закрытия отделкой.
7. Расчёт нагрузок, токов КЗ, селективности и сечений — по проекту ЭОМ организации с допуском СРО; лист задаёт состав, расположение и группы.
8. Ведомость светильников (тип, количество, мощность, поток, Tц, Ra) — лист 58.

					Проект: Дом 120 м² — М 1:50
	Лист	№ док.	Подпись	Дата	План освещения · 2-й этаж
Дизайнер	Кырлан А.С.			04.11.26	Стадия: П; Лист: 57; Листов: 136

выпуск 04.11.2026 № 406ed8a6ce · стр. 57 из 136

Параметры светильников для подбора

Поз.	Марки	Наименование	Установка	Кол.	P, Вт	Σ P, Вт	Ф, лм	Тц, К	Ra	Угол, °	IP	Дим.	Слой	Группа	Пом.
1	Св31–Св40	Встраиваемый точечный	в ГКЛ, корпус ≤ 70 мм	10	12	120	1000	3000	90	—	20	да	общий	L12	1
2	Св41	Лента светодиодная 24 В	в карнизе короба, профиль с рассеивателем	20,5 м	9,6/м	196,4	900/м	2700	90	—	20	да	акцентный	L13	1
3	Св42, Св43, Св44	Подвесной	подвес, низ H=1450	3	9	27	800	3000	90	—	20	да	общий	L14	1
4	Св45–Св48	Встраиваемый точечный	в ГКЛ, корпус ≤ 70 мм	4	10	40	900	3000	90	—	20	да	общий	L15	1
5	Св49	Линейный настенный	под верхними шкафами, H=1440	1	18	18	1500	3000	90	—	20	да	рабочий	L16	1
6	Св26–Св29, Св53, Св54, Св82–Св85, Св93, Св94	Встраиваемый точечный	в ГКЛ, корпус ≤ 70 мм	12	7	84	600	3000	90	—	20	—	общий	L10, L84	2, 5, 10, 11
7	Св80	Подвесной	подвес	1	12	12	1100	3000	90	—	20	—	общий	L80	2
8	Св17–Св22	Встраиваемый точечный	в ГКЛ, корпус ≤ 70 мм	6	14	84	1400	2700	90	—	20	—	общий	L7	3
9	Св23	Лента светодиодная 24 В	в нише уровня, профиль с рассеивателем	5,7 м	9,6/м	54,7	900/м	2700	90	—	20	да	акцентный	L8	3
10	Св50	Встраиваемый точечный	в ГКЛ, корпус ≤ 70 мм	1	7	7	600	3000	90	—	44	—	общий	L17	4
11	Св12–Св14, Св51	Встраиваемый точечный	в ГКЛ, корпус ≤ 70 мм	4	6	24	500	3000	90	—	44	—	общий	L4, L17	4, 13
12	Св15, Св52	Настенный светильник над зеркалом, драйвер встроен	над зеркалом, H=1900	2	8	16	600	3000	90	—	44	—	рабочий	L5, L18	4, 13
13	Св30	Лента светодиодная 24 В	на поверхности, профиль с рассеивателем, датчик движения	1,8 м	4,8/м	8,6	150/м	2700	90	—	20	нет	ночной	L11	5
14	Св1–Св8	Встраиваемый точечный	в ГКЛ, корпус ≤ 70 мм	8	12	96	1000	2700	90	—	20	—	общий	L1	6
15	Св9	Лента светодиодная 24 В	в нише уровня, профиль с рассеивателем	4,5 м	9,6/м	43,1	900/м	2700	90	—	20	да	акцентный	L2	6
16	Св10, Св11, Св24, Св102	Настенный (бра)	на стене, H=1500	4	6	24	400	2700	90	60	20	—	рабочий	L3, L9	6, 7, 12
17	Св86–Св91, Св95–Св100	Встраиваемый точечный	в ГКЛ, корпус ≤ 70 мм	12	11	132	1100	2700	90	—	20	—	общий	L7	7, 12
18	Св92	Лента светодиодная 24 В	в карнизе короба, профиль с рассеивателем	12 м	9,6/м	114,8	900/м	2700	90	—	20	да	акцентный	L8	7
19	Св16	Потолочный накладной	на потолке, засветка стены	1	10	10	900	3000	90	—	20	—	общий	L6	8
20	Св25	Потолочный накладной	на потолке	1	9	9	600	3000	90	—	20	—	общий	L3	9
21	Св101	Лента светодиодная 24 В	в карнизе короба, профиль с рассеивателем	10,1 м	9,6/м	96,6	900/м	2700	90	—	20	да	акцентный	L8	12
		Итого		**70 шт + 54,5 м**		**1217,3**									

LED-ленты, линейные светильники и блоки питания

Марка	Пом.	L, м	U, В	Вт/м	Σ P, Вт	БП	P БП, Вт	Загр., %	Питание	Доступ к БП
Св41	1	20,5	24	9,6	196,4	БП4	300	65	с двух концов	люк 300×300 в коробе потолка ПТ1
Св49	1	3	24	—	18	БП5	60	30	встроенный ввод	в пенале M_09, верх, съёмная панель
Св23	3	5,7	24	9,6	54,7	БП2	200	27	с двух концов	люк 300×300 в нише фигуры потолка ПТ4
Св30	5	1,8	24	4,8	8,6	БП3	20	43	с одного конца	в шкафу M_24, верхняя полка
Св9	6	4,5	24	9,6	43,1	БП1	200	22	с двух концов	люк 300×300 в нише фигуры потолка ПТ6
Св92	7	12	24	9,6	114,8	БП6	200	57	с двух концов	люк 300×300 в коробе потолка ПТ8
Св101	12	10,1	24	9,6	96,6	БП7	200	48	с двух концов	люк 300×300 в коробе потолка ПТ8

Сценарии (помещения со светорегуляторами)


Помещение	Сценарий	Горят группы (уровень)	Управление
1. Гостиная-кухня	Вечер	L12 споты гостиной — 30 %; L13 подсветка короба — 100 %; L14 подвесы над столом — 50 %; остальные выкл.	светорегуляторы S9, S10
	Ужин	L13 подсветка короба — 60 %; L14 подвесы над столом — 100 %; L16 подсветка столешницы — 30 %; остальные выкл.	светорегуляторы S9, S10, S11
	Кино	L13 подсветка короба — 20 %; остальные выкл.	светорегулятор S9
	Готовка	L12 споты гостиной — 50 %; L15 споты кухни — 100 %; L16 подсветка столешницы — 100 %; остальные выкл.	светорегуляторы S9, S10, S11

Примечания

1. Позиции и марки Св — те же, что на плане освещения (листы 56, 57); группы L — по плану выключателей (листы 59, 60).
2. Модели светильников не выбраны: лист — техническое задание на подбор. Модель по строке таблицы: поток, Тц, Ra, угол, IP и регулировка яркости не хуже указанных, мощность не больше; встраиваемые — под глубину короба (графа «Установка»). IP 20 — сухие помещения. После выбора моделей (артикул, производитель) лист выпускается как «Спецификация светильников».
3. Длина LED-ленты в карнизе и нише уровня — по линиям карниза и ниши плана потолков (листы 43, 44); Σ P = Вт/м × длина. Блок питания загружен не больше чем на 80 %; лента 24 В длиннее 10 м питается с двух концов; доступ к блоку питания — люк ревизии 300×300 мм или место, указанное в таблице.
4. Сценарии: % — яркость группы на светорегуляторе; «вкл.» — группа на обычной клавише; группы, не названные в строке, выключены. Светильники и блоки питания групп на светорегуляторе — с регулировкой яркости. Клавиши и светорегуляторы — листы 59, 60.
5. В пом. 3, 6, 7, 12 свет включается клавишами групп — листы 59, 60.
6. Мощность и поток в таблице — требования к подбору (поток не меньше, мощность не больше указанных); после выбора модели — по её паспорту, Σ P — установленная мощность освещения. Оценка освещённости — на плане освещения; это не светотехнический расчёт.

					Проект: Дом 120 м²
	Лист	№ док.	Подпись	Дата	Техническое задание на подбор светильников
Дизайнер	Кырлан А.С.			04.11.26	

Стадия	Лист	Листов
П	58	136

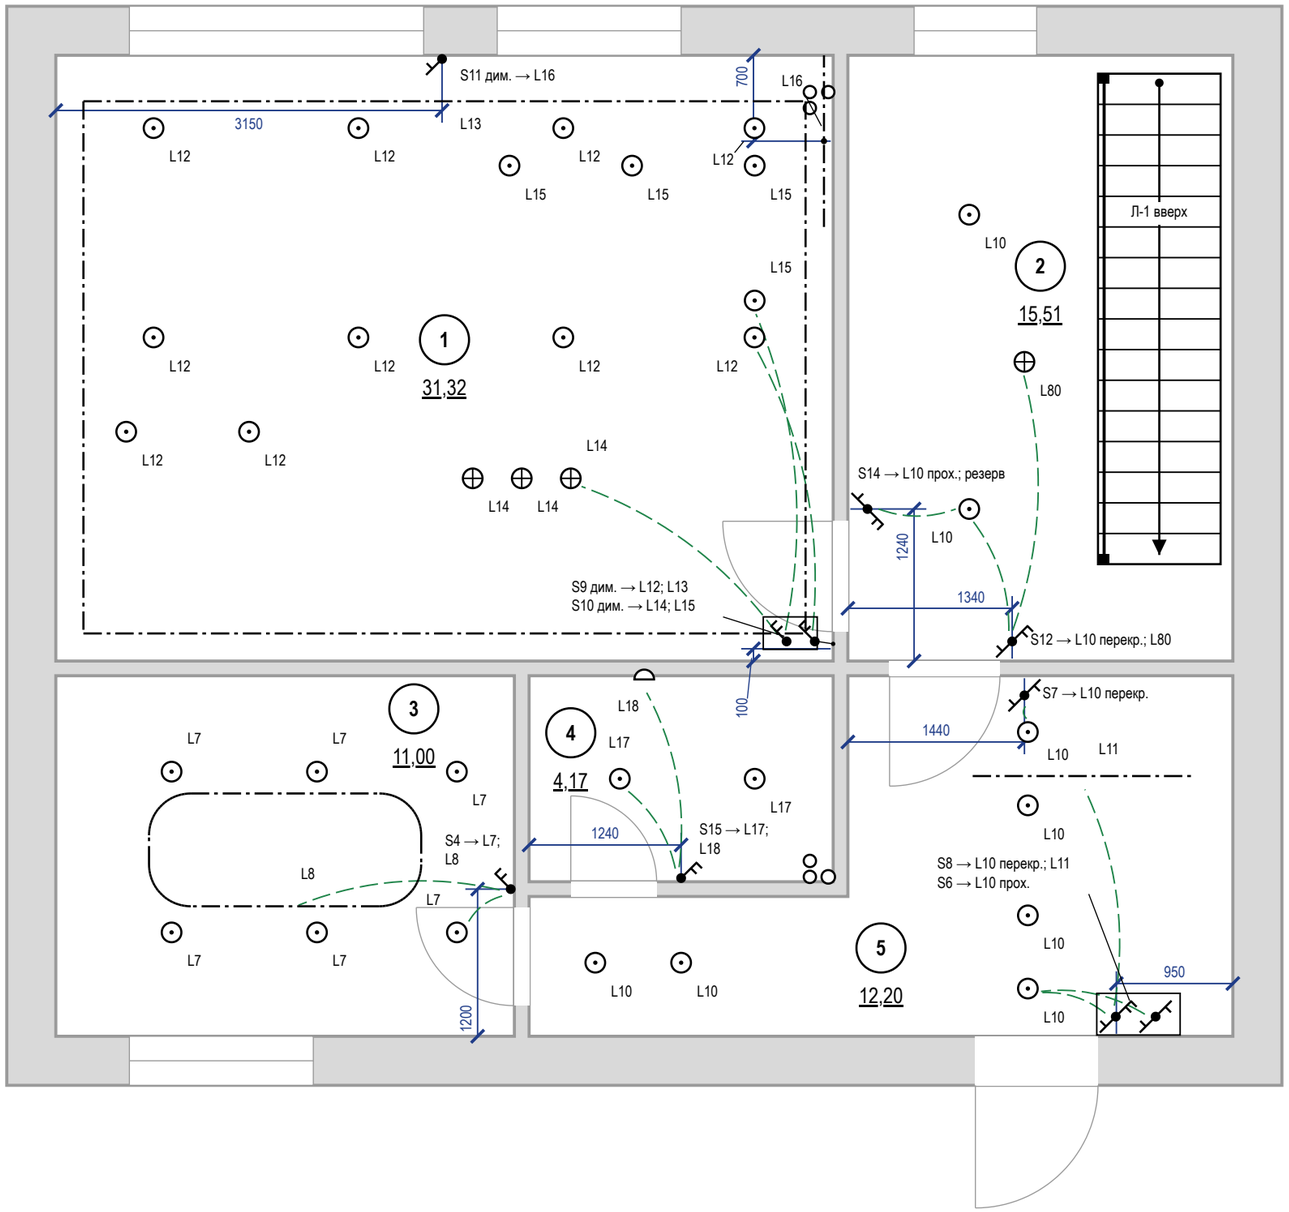

Условные обозначения


- выключатель одноклавишный
- выключатель двухклавишный (флажков — по числу клавиш)
- выключатель с проходной или перекрёстной клавишей (обратный флажок); тип клавиши — в подписи
- S1 → — марка → группы по клавишам (через «;»): прох. проходной, перекр. — перекрёстный, дим. светорегулятор; Н — высота
- связь: выключатель → ближайший светильник группы в том же помещении (не трасса кабеля); полный состав группы — по номеру L
- светильник встраиваемый точечный
- светильник подвесной
- светильник настенный (бра), Н — высота оси
- линейный светильник настенный (подсветка столешницы), точка — вывод питания
- светодиодная лента в профиле / в карнизе короба
- L1 — группа включения у светильника
- стояк: К1 — канализация, В1 — ХВС, Т3 — ГВС
- 1 — номер помещения, площадь м²

Примечания

1. За отметку 0,000 принят уровень чистого пола. Высоты Н — от чистого пола до оси изделия; привязки — от чистовой грани стены до оси механизма (у рамки на несколько постов — до оси рамки).
2. Высота установки, не указанная на плане: выключатели — 900 мм от чистого пола (у кровати и другие — Н у марки), со стороны дверной ручки (ПУЭ 7.1.51).
3. Какой выключатель какие светильники включает — по номеру группы L: у выключателя (S1 → L1; L2 — клавиши по порядку) и у каждого светильника. Пунктир подсказка к ближайшему светильнику группы в том же помещении (не дальше 3 м), это не трасса кабеля; выключатель за стеной (у двери санузла) и далёкая группа — только номер группы.
4. Группы из нескольких мест (L10 — S6, S7, S8, S12, S14): на крайних местах — проходные клавиши, на промежуточных — перекрёстные; механизмы — в ведомости изделий.
5. Светорегулятор — по заднему фронту (для LED-драйверов), совместимость с драйверами проверить до закупки.
6. Розеточные и мокрые линии — через УЗО или дифавтомат с током утечки не более 30 мА (ПУЭ 7.1.79); в санузле выполнить ДСУП (ПУЭ 7.1.87–7.1.88).
7. Кабель — медный, исполнение нг(A)-LS (ГОСТ 31565-2012); скрытая прокладка только горизонтально и вертикально, фактические трассы зафиксировать исполнительной схемой до закрытия отделкой.
8. Расчёт нагрузок, токов КЗ, селективности и сечений — по проекту ЭОМ организации с допуском СРО; лист задаёт состав, расположение и группы.

					Проект: Дом 120 м²	М 1:50
	Лист	№ док.	Подпись	Дата	Управление светильниками · 1-й этаж	Стадия / Лист / Листов
Дизайнер	Кырлан А.С.			04.11.26		П / 59 / 136

выпуск 04.11.2026 № 406ed8a6ce · стр. 59 из 136

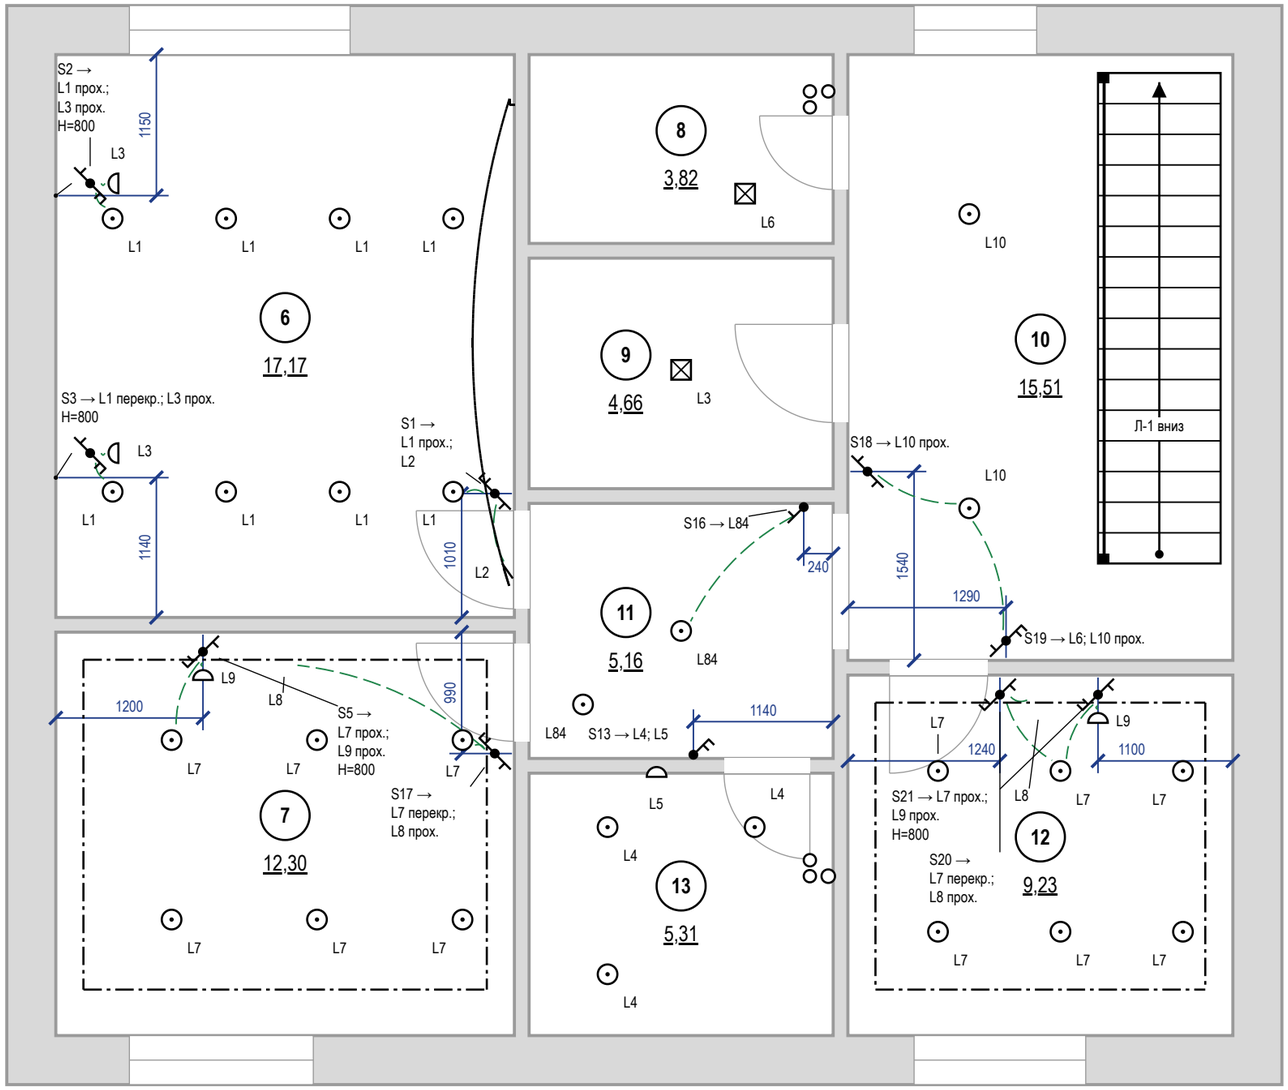


Условные обозначения

- выключатель одноклавишный
- выключатель двухклавишный (флажков — по числу клавиш)
- выключатель с проходной или перекрёстной клавишей (обратный флажок); тип клавиши — в подписи
- S1 → — марка → группы по клавишам (через «;»): прох. проходной, перекр. — перекрёстный, дим. светорегулятор; H — высота
- связь: выключатель → ближайший светильник группы в том же помещении (не трасса кабеля); полный состав группы — по номеру L
- светильник встраиваемый точечный
- светильник потолочный накладной
- светильник настенный (бра), H — высота оси
- светодиодная лента в профиле / в карнизе короба
- L1 — группа включения у светильника
- стояк: К1 — канализация, В1 — ХВС, Т3 — ГВС
- 1 — номер помещения, площадь м²

Примечания

1. За отметку 0,000 принят уровень чистого пола. Высоты H — от чистого пола до оси изделия; привязки — от чистовой грани стены до оси механизма (у рамки на несколько постов — до оси рамки).
2. Высота установки, не указанная на плане: выключатели — 900 мм от чистого пола (у кровати и другие — H у марки), со стороны дверной ручки (ПУЭ 7.1.51).
3. Какой выключатель какие светильники включает — по номеру группы L: у выключателя (S1 → L1; L2 — клавиши по порядку) и у каждого светильника. Пунктир подсказка к ближайшему светильнику группы в том же помещении (не дальше 3 м), это не трасса кабеля; выключатель за стеной (у двери санузла) и далёкая группа — только номер группы.
4. Группы из нескольких мест (L1 — S1, S2, S3; L3 — S2, S3; L7 — S5, S17, S20, S21; L8 — S17, S20; L9 — S5, S21; L10 — S18, S19): на крайних местах — проходные клавиши, на промежуточных — перекрёстные; механизмы — в ведомости изделий.
5. Розеточные и мокрые линии — через УЗО или дифавтомат с током утечки не более 30 мА (ПУЭ 7.1.79); в санузле выполнить ДСУП (ПУЭ 7.1.87–7.1.88).
6. Кабель — медный, исполнение нг(А)-LS (ГОСТ 31565-2012); скрытая прокладка только горизонтально и вертикально, фактические трассы зафиксировать исполнительной схемой до закрытия отделкой.
7. Расчёт нагрузок, токов КЗ, селективности и сечений — по проекту ЭОМ организации с допуском СРО; лист задаёт состав, расположение и группы.

					Проект: Дом 120 м²	М 1:50
	Лист	№ док.	Подпись	Дата		
Дизайнер	Кырлан А.С.			04.11.26	Управление светильниками · 2-й этаж	Стадия: П; Лист: 60; Листов: 136

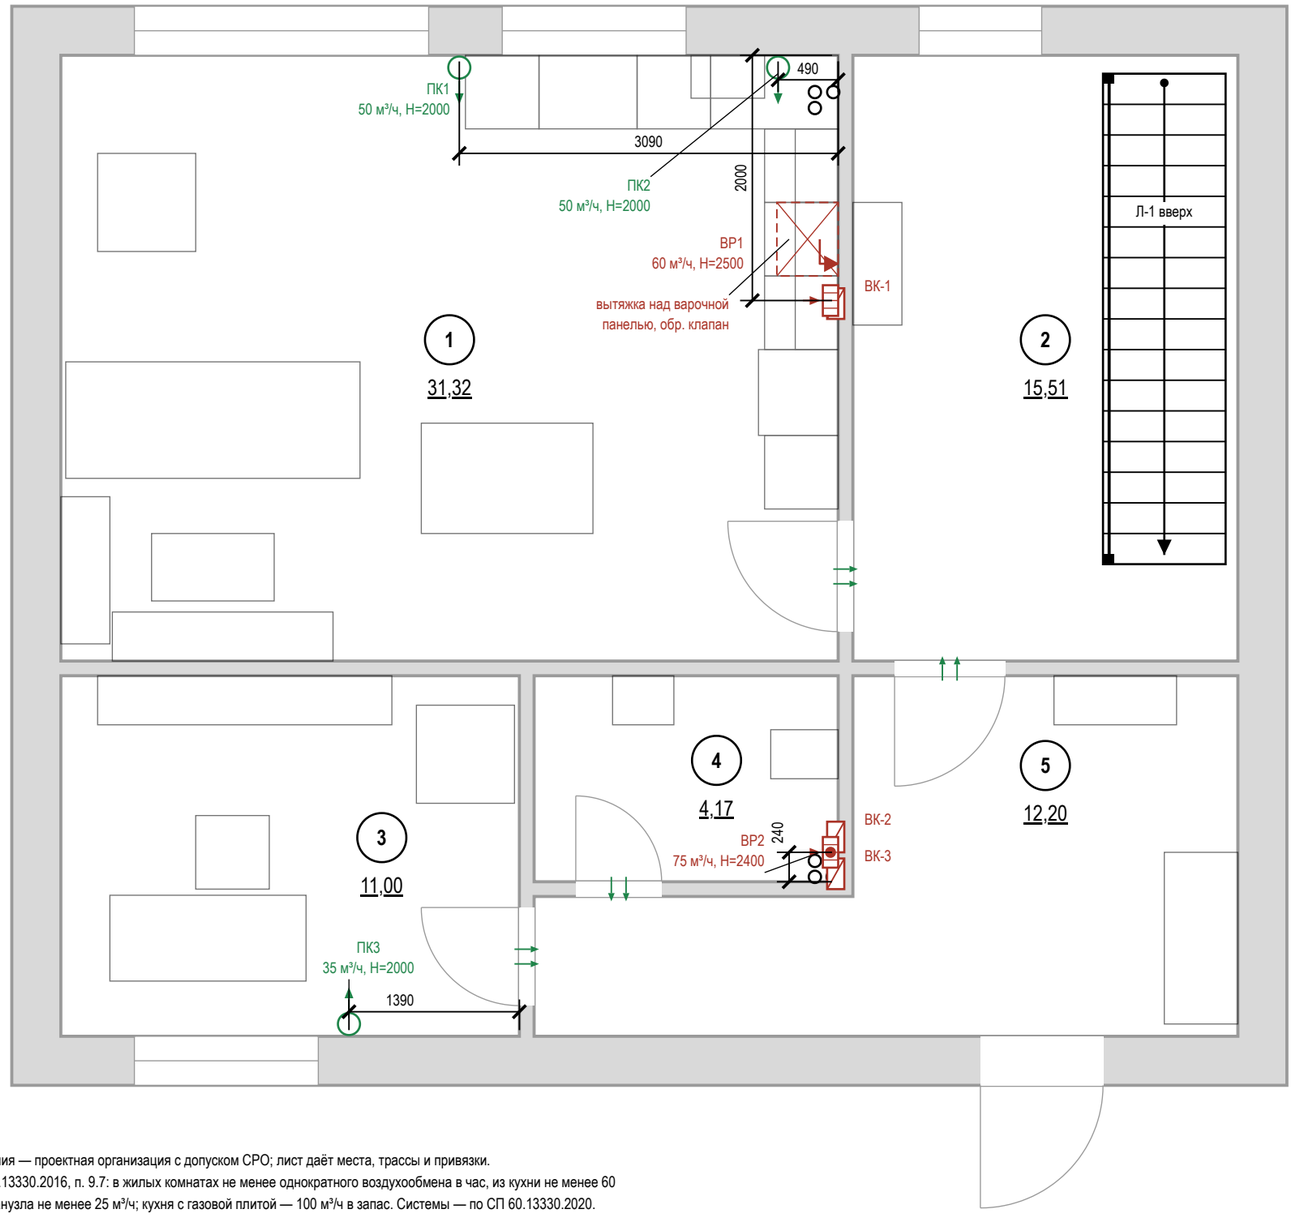

Условные обозначения

- стояк: К1 — канализация, В1 — ХВС, Т3 — ГВС
- номер помещения, площадь м²
- вытяжная решётка в вентканал: марка, расход м³/ч, Н центра от чистого пола
- вытяжная решётка с бытовым вентилятором и обратным клапаном: марка, расход, Н
- приточный клапан (КИВ) в наружной стене: марка, расход, Н центра
- переток: зазор под полотном или переточная решётка
- кухонная вытяжка над варочной панелью
- Вентканал ВК-N.
- воздуховод кухонной вытяжки в коробе под потолком
- отдельный вход воздуховода в вентканал, обратный клапан

Воздухообмен, м³/ч

№	Помещение	Выт. норма	Выт. проект	Прит. норма	Прит. проект	Устрой-ства
1	Гостиная-кухня	60	60	91	100	ВР1, ПК1, ПК2
3	Кабинет			32	35	ПК3
4	Санузел гостевой	25	75			ВР2
	Итого	**85**	**135**	**123**	**135**	


Воздухообмен этажа — по большей из сумм притока и вытяжки:
норма 123 м³/ч, проект 135 м³/ч.
Вытяжка не меньше притока — баланс сведён.

Привязки — до обмера
Вентканалы ВК-N приняты проектировщиком, решётки и воздуховоды — от них. До черновых работ — обмер каналов и тяги, лист перевыпустить по факту.

Примечания

1. Расчёт систем ОВ и подбор оборудования — проектная организация с допуском СРО; лист даёт места, трассы и привязки.
2. Нормы одноквартирного дома — СП 55.13330.2016, п. 9.7: в жилых комнатах не менее однократного воздухообмена в час, из кухни не менее 60 м³/ч, из ванной, туалета, совмещённого санузла не менее 25 м³/ч; кухня с газовой плитой — 100 м³/ч в запас. Системы — по СП 60.13330.2020.
3. Вентканалы и шахты не сужать, не переносить и не закрывать; вентилятор и кухонная вытяжка — через обратный клапан, без перекрытия естественной тяги.
4. Проектные расходы — не ниже нормы, вытяжка сведена с притоком вентиляторами мокрых помещений. Клапаны — в простенке у окна, центр 2000 мм, не над кроватью, не ближе 300 мм к стоякам отопления; типоразмер — на расход.
5. Кухонная вытяжка в воздухообмен не включена: воздуховод не менее Ø125 в коробе, вход в канал отдельный.
6. Переток — зазор под полотнами межкомнатных дверей или переточная решётка.
7. Кондиционирование заданием не предусмотрено; при установке трассы фреона и дренажа (не менее 40 мм/м, в К1 через сифон) и питание заложить до черновых работ.
8. Привязки оборудования — по паспортам приобретённых моделей, до черновых работ.

					Проект: Дом 120 м² — **М 1:50**
	Лист	№ док.	Подпись	Дата	План вентиляции · 1-й этаж — Стадия: П; Лист: 61; Листов: 136
Дизайнер	Кырлан А.С.			04.11.26	

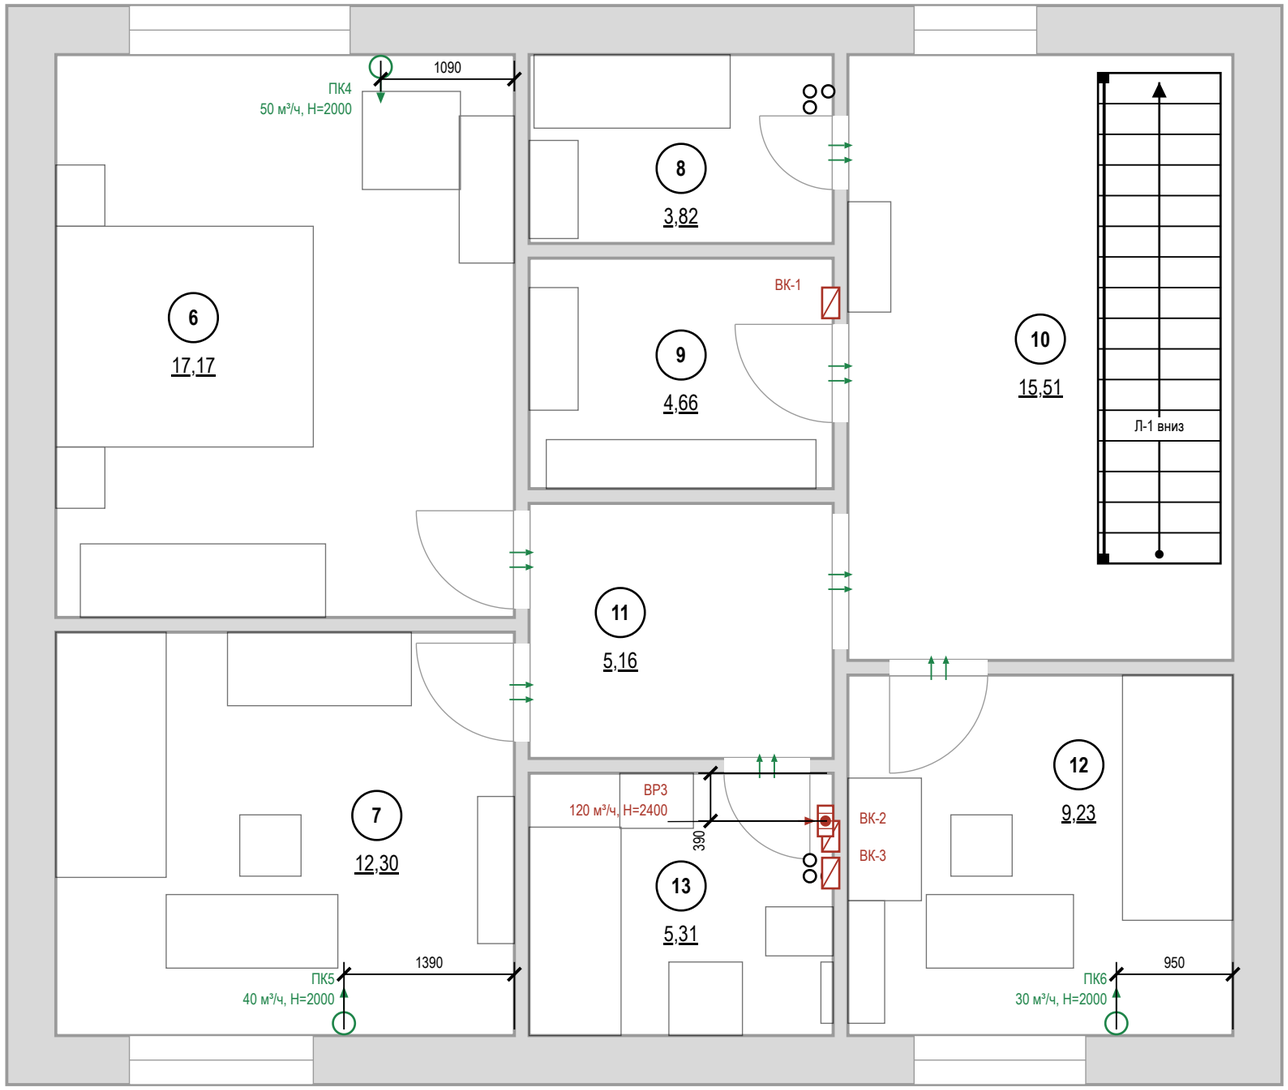

Условные обозначения

- стояк: К1 — канализация, В1 — ХВС, Т3 — ГВС
- 1 — номер помещения, площадь м²
- вытяжная решётка с бытовым вентилятором и обратным клапаном: марка, расход, Н
- приточный клапан (КИВ) в наружной стене: марка, расход, Н центра
- переток: зазор под полотном или переточная решётка
- Вентканал ВК-N.

Воздухообмен, м³/ч

№	Помещение	Выт. норма	Выт. проект	Прит. норма	Прит. проект	Устрой-ства
6	Спальня родителей			50	50	ПК4
7	Детская			36	40	ПК5
8	Гардеробная	2				переток
9	Кладовая	3				переток
12	Детская вторая			27	30	ПК6
13	Санузел второго этажа	25	120			ВР3
	Итого	**30**	**120**	**113**	**120**	

Воздухообмен этажа — по большей из сумм притока и вытяжки: норма 113 м³/ч, проект 120 м³/ч.
Вытяжка не меньше притока — баланс сведён.


Привязки — до обмера
Вентканалы ВК-N приняты проектировщиком, решётки и воздуховоды — от них. До черновых работ — обмер каналов и тяги, лист перевыпустить по факту.

Примечания

1. Расчёт систем ОВ и подбор оборудования — проектная организация с допуском СРО; лист даёт места, трассы и привязки.
2. Нормы одноквартирного дома — СП 55.13330.2016, п. 9.7: в жилых комнатах не менее однократного воздухообмена в час, из кухни не менее 60 м³/ч, из ванной, туалета, совмещённого санузла не менее 25 м³/ч; кухня с газовой плитой — 100 м³/ч в запас. Системы — по СП 60.13330.2020.
3. Вентканалы и шахты не сужать, не переносить и не закрывать; вентилятор и кухонная вытяжка — через обратный клапан, без перекрытия естественной тяги.
4. Проектные расходы — не ниже нормы, вытяжка сведена с притоком вентиляторами мокрых помещений. Клапаны — в простенке у окна, центр 2000 мм, не над кроватью, не ближе 300 мм к стоякам отопления; типоразмер — на расход.
5. Переток — зазор под полотнами межкомнатных дверей или переточная решётка.
6. Кондиционирование заданием не предусмотрено; при установке трассы фреона и дренажа (не менее 40 мм/м, в К1 через сифон) и питание заложить до черновых работ.
7. Привязки оборудования — по паспортам приобретённых моделей, до черновых работ.

					Проект: Дом 120 м² — **М 1:50**
	Лист	№ док.	Подпись	Дата	
Дизайнер	Кырлан А.С.			04.11.26	План вентиляции · 2-й этаж

Стадия	Лист	Листов
П	62	136

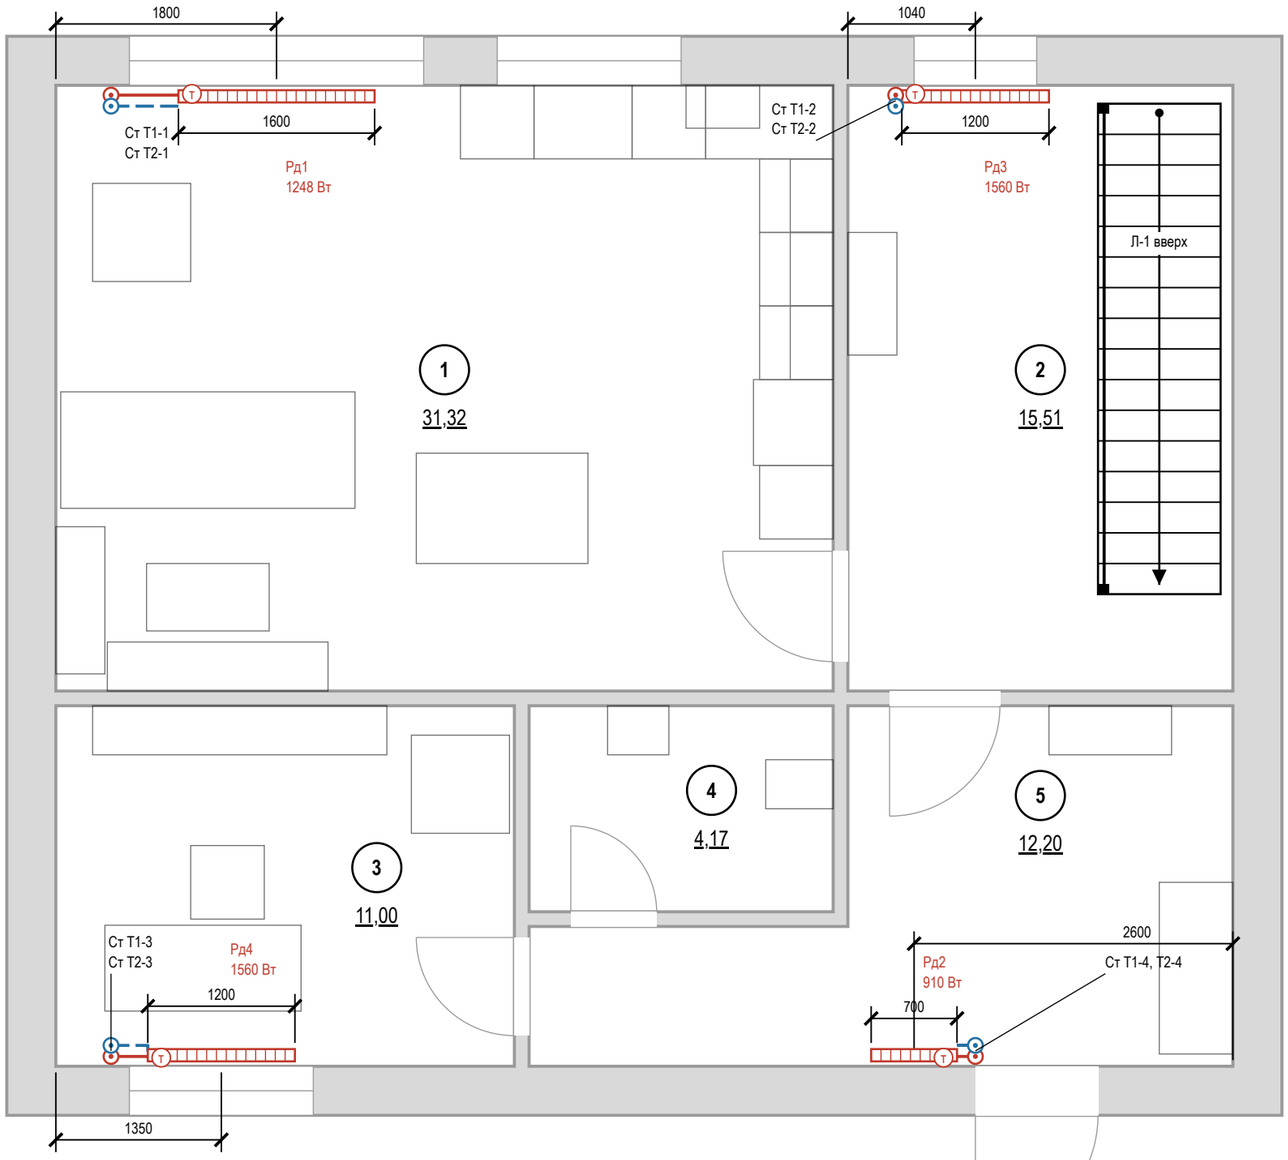

Условные обозначения

- (1) — номер помещения, площадь м²
- радиатор отопления (марка РО-N, длина по плану)
- (Т) — клапан с термоголовкой на подаче
- стояк отопления, подающий (Ст Т1-N)
- стояк отопления, обратный (Ст Т2-N)
- Т1 — отопление, подающий трубопровод
- Т2 — отопление, обратный трубопровод

Ведомость радиаторов

Марка	Помещение	Тип	Д×В×Г, мм	Низ / стена	Q, Вт
Рд1	1. Гостиная-кухня	панельный 22	1600×300×100	100 / 40	1248
Рд3	2. Холл с лестницей	панельный 22	1200×500×100	100 / 40	1560
Рд4	3. Кабинет	панельный 22	1200×500×100	100 / 40	1560
Рд2	5. Прихожая	панельный 22	700×500×100	100 / 40	910

Низ — от чистого пола, стена — зазор до задней панели, мм.


Привязки — до обмера
Подъёмы подводок отопления в исходных данных не заданы: показаны у откосов окон и у торцов приборов принципиально, разводка — от котла через распределительный коллектор. До черновых работ — место котла, коллектора и подъёмов труб и паспорта приборов; лист перевыпустить по факту.

Примечания

1. Расчёт системы отопления, теплопотерь и подбор приборов — проектная организация с допуском СРО; лист даёт места и привязки.
2. Тип, длина и мощность радиаторов — по теплотехническому расчёту; лист задаёт места, зазоры и подключение.
3. Зазоры радиатора: низ не менее 100 мм от чистого пола, верх не менее 100 мм до подоконника, 30–50 мм от стены до задней панели; центр по оси окна с допуском ±20 мм. Верх до подоконника — 300 мм (Рд1 — 100). Радиаторы не закрывать глухими коробами и мебелью; трубы через стены и перекрытия — в гильзах.
4. Источник тепла (котёл: газ / электро / твёрдое топливо), его место и котельная — по решению заказчика; до решения разводка от коллектора к приборам — принципиальная (СП 60.13330.2020).
5. Без отопительного прибора: пом. 4 — внутренние, без наружных стен, окон и дверей наружу, обогреваются от смежных помещений; полотенцесушитель — по листам ВК.
6. Привязки приборов и подводок — по паспортам приобретённых радиаторов и клапанов, до черновых работ.
7. До закрытия отделкой трубопроводы отопления испытать гидростатическим давлением с оформлением акта (СП 73.13330.2016, 7.2–7.3).

					Проект: Дом 120 м²	М 1:50
	Лист	№ док.	Подпись	Дата		
Дизайнер	Кырлан А.С.			04.11.26	План отопления · 1-й этаж	

Стадия	Лист	Листов
П	63	136

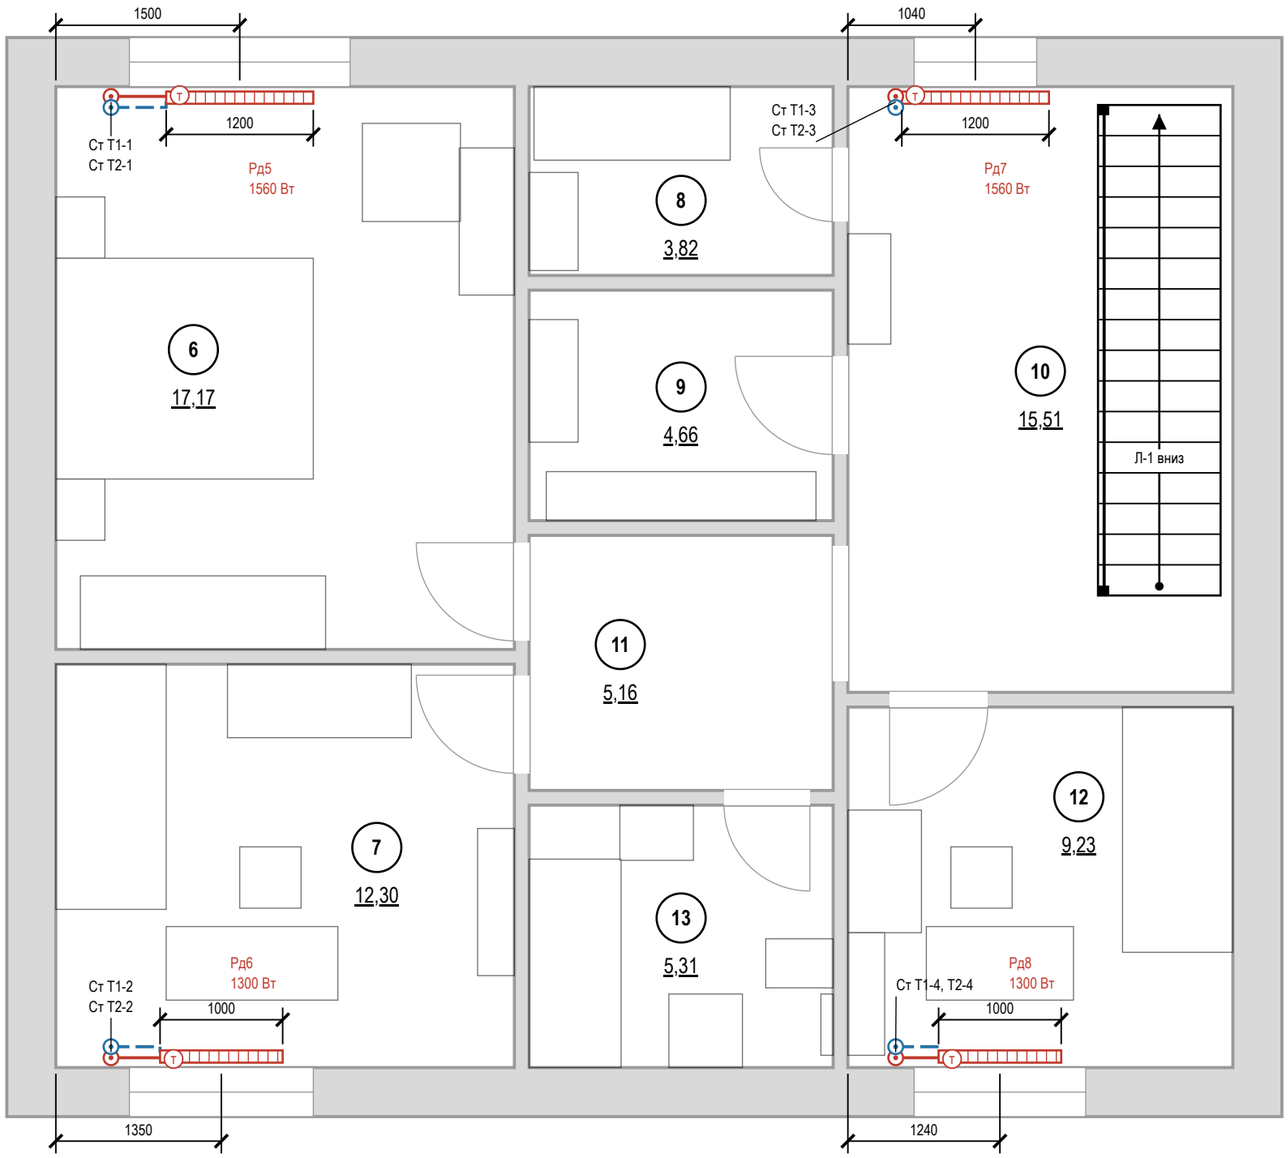

Условные обозначения

- (1) — номер помещения, площадь м²
- радиатор отопления (марка РО-N, длина по плану)
- (Т) — клапан с термоголовкой на подаче
- стояк отопления, подающий (Ст Т1-N)
- стояк отопления, обратный (Ст Т2-N)
- Т1 — отопление, подающий трубопровод
- Т2 — отопление, обратный трубопровод

Ведомость радиаторов

Марка	Помещение	Тип	Д×В×Г, мм	Низ / стена	Q, Вт
Рд5	6. Спальня родителей	панельный 22	1200×500×100	100 / 40	1560
Рд6	7. Детская	панельный 22	1000×500×100	100 / 40	1300
Рд7	10. Холл второго этажа	панельный 22	1200×500×100	100 / 40	1560
Рд8	12. Детская вторая	панельный 22	1000×500×100	100 / 40	1300


Низ — от чистого пола, стена — зазор до задней панели, мм.

Привязки — до обмера
Подъёмы подводок отопления в исходных данных не заданы: показаны у откосов окон принципиально, разводка — от котла через распределительный коллектор. До черновых работ место котла, коллектора и подъёмов труб и паспорта приборов; лист перевыпустить по факту.



Примечания

1. Расчёт системы отопления, теплопотерь и подбор приборов — проектная организация с допуском СРО; лист даёт места и привязки.
2. Тип, длина и мощность радиаторов — по теплотехническому расчёту; лист задаёт места, зазоры и подключение.
3. Зазоры радиатора: низ не менее 100 мм от чистого пола, верх не менее 100 мм до подоконника, 30–50 мм от стены до задней панели; центр по оси окна с допуском ±20 мм. Верх до подоконника — 300 мм. Радиаторы не закрывать глухими коробами и мебелью; трубы через стены и перекрытия в гильзах.
4. Источник тепла (котёл: газ / электро / твёрдое топливо), его место и котельная — по решению заказчика; до решения разводка от коллектора к приборам — принципиальная (СП 60.13330.2020).
5. Без отопительного прибора: пом. 9, пом. 11 — внутренние, без наружных стен, окон и дверей наружу, обогреваются от смежных помещений; полотенцесушитель — по листам ВК.
6. Прибор не задан: пом. 13 — прибор или тёплый пол по расчёту до черновых работ.
7. Привязки приборов и подводок — по паспортам приобретённых радиаторов и клапанов, до черновых работ.
8. До закрытия отделкой трубопроводы отопления испытать гидростатическим давлением с оформлением акта (СП 73.13330.2016, 7.2–7.3).

					Проект: Дом 120 м² — М 1:50
	Лист	№ док.	Подпись	Дата	План отопления · 2-й этаж
Дизайнер	Кырлан А.С.			04.11.26	Стадия: П; Лист: 64; Листов: 136

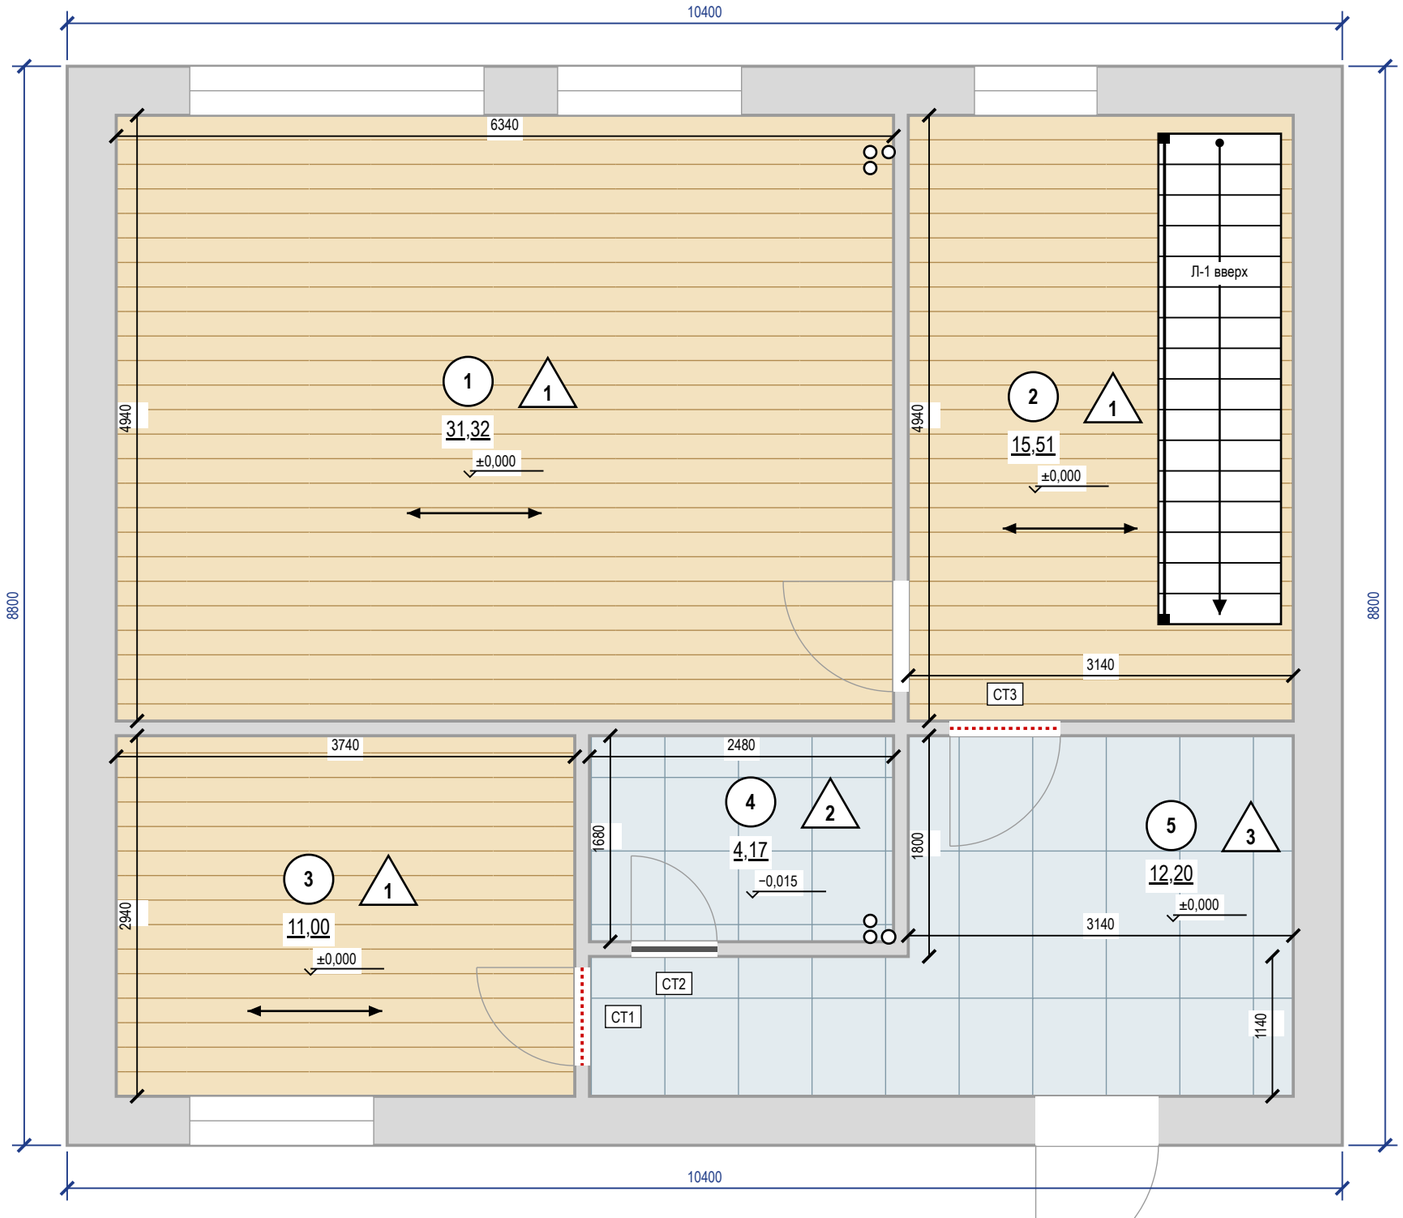

Экспликация полов

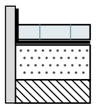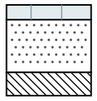Пом.	Тип пола	Схема пола	Элементы пола, толщина, мм	Площадь, м²
1, 2, 3	1		Инженерная доска на клею — 14 Стяжка ЦПС М200 — 50 Плита перекрытия Всего 64 мм; ЧП ±0,000, верх плиты −0,064	57,83
4	2		Керамогранит на клею С2 TE S1 — 14 Гидроизоляция обмазочная, 2 слоя, с заведением на стены 200 мм — 2 Стяжка ЦПС М200 — 33 Плита перекрытия Всего 49 мм; ЧП −0,015, верх плиты −0,064	4,17
5	3		Керамогранит на клею С2 TE S1 — 14 Стяжка ЦПС М200 — 50 Плита перекрытия Всего 64 мм; ЧП ±0,000, верх плиты −0,064	12,20
			Итого	**74,20**

Раскладка покрытий

Пом.	Укладка	Старт (оси от чистовых стен), мм	Отступ 1-го ряда / крайние плитки, мм
1	вдоль стен A/B, прямая	от стены А, 1-й ряд вдоль неё	зазор от стены не задан
2	вдоль стен A/B, прямая	от стены А, 1-й ряд вдоль неё	зазор от стены не задан
3	вдоль стен A/B, прямая	от стены В, 1-й ряд вдоль неё	зазор от стены не задан
4	прямая, сетка 600×600, шов 2	ось X 1216 от Г; ось Y 816 от А	X 312 / 312; Y 514 / 514
5	плитка	раскладка плиточника не задана	

Спецификация плинтусов

Наименование	Помещения	Длина, м (с запасом)
Плинтус МДФ под покраску 80×16, крепление к стене, окраска в цвет Tikkurila G503	1, 2, 3, 5	69

Отметки по высоте

±0,000	чистый пол пом. 1–3, 5; отсчёт высот
−0,015	чистый пол пом. 4, ниже на 15 мм
−0,064	верх плиты — расчёт, не замер (задание на обмер)
сущ. пол	снимается до плиты; не замерен (задание на обмер)

Примечания


1. За отметку ±0,000 принят чистый пол 1-го этажа, не существующий (блок отметок). Площади — по чистым размерам помещений, м²; размеры — в мм.
2. Стык разнотипных покрытий — по оси дверного полотна (под полотном в закрытом положении); решение стыка — по ведомости стыков.
3. Размеры помещений в свету (ширина × длина, мм), не поместившиеся на плане: пом. 5 — 3140 × 1800, 5740 × 1140.
4. Пол санузлов ниже смежных помещений на 15 мм за счёт меньшей толщины стяжки (верх плиты общий — по экспликации полов); гидроизоляция по стяжке с заведением на стены не менее 200 мм (СП 29.13330.2011, п. 7.2), до облицовки — тест проливом и акт скрытых работ.
5. Трубопроводы в конструкции пола не прокладываются: пирог пола 49–64 мм не вмещает выпуски канализации с уклоном — выпуски К1 ведутся по стенам над чистым полом в коробах.
6. Штучные покрытия (инженерная доска): направление — по стрелке; влажность основания по СМ не более 2,0 % (по ТУ изготовителя).
7. Ровность основания — просвет под 2-метровой рейкой не более 2 мм: пом. 1, 2, 3 (инженерная доска), пом. 4, 5 (керамогранит); проверить до укладки покрытия (СП 71.13330.2017, табл. 8.5).
8. Сетка на плитке — условная, в размер формата; точка старта и раскладка — по листу раскладки плитки.
9. Узор покрытия (заливка-код типа пола) прерывается под надписями — площадями помещений и отметками чистого пола.
10. Пироги полов — по экспликации полов: слои сверху вниз, толщины в мм; гидроизоляция мокрых зон — в пироге и в ведомости отделки; схема пола — без масштаба.

					Проект: Дом 120 м² — **М 1:50**
	Лист	№ док.	Подпись	Дата	
Дизайнер	Кырлан А.С.			04.11.26	План покрытий пола · 1-й этаж



Стадия	Лист	Листов
П	65	136

Отметки по высоте

±0,000 чистый пол 1-го этажа; отсчёт отметок
+3,230 чистый пол пом. 6–12 (2-й этаж)
+3,215 чистый пол пом. 13, ниже на 15 мм
+3,166 верх плиты — расчёт, не замер (задание на обмер)
сущ. пол снимается до плиты; не замерен (задание на обмер)

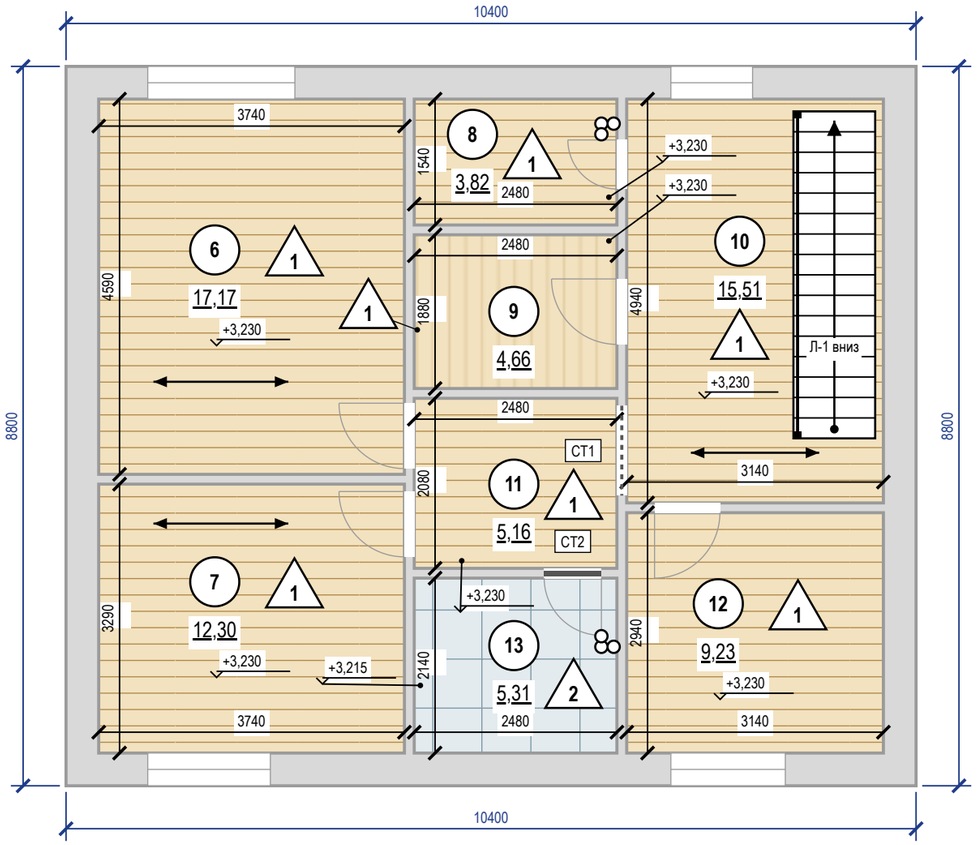

Экспликация полов

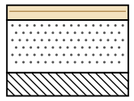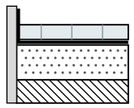Номер помещения	Тип пола	Схема пола	Данные элементов пола (наименование, толщина, основание), мм	Площадь, м²
6, 7, 8, 9, 10, 11, 12	1		Инженерная доска на клею — 14 Стяжка ЦПС М200 — 50 Плита перекрытия Всего 64 мм; ЧП +3,230, верх плиты +3,166	67,85
13	2		Керамогранит на клею С2 TE S1 — 14 Гидроизоляция обмазочная, 2 слоя, с заведением на стены 200 мм — 2 Стяжка ЦПС М200 — 33 Плита перекрытия Всего 49 мм; ЧП +3,215, верх плиты +3,166	5,31
			Итого	**73,16**

Раскладка покрытий

Пом.	Укладка	Старт (оси от чистовых стен), мм	Отступ 1-го ряда / крайние плитки, мм
6	вдоль стен А/В, прямая	от стены А, 1-й ряд вдоль неё	зазор от стены не задан
7	вдоль стен А/В, прямая	от стены В, 1-й ряд вдоль неё	зазор от стены не задан
8	вдоль стен А/В, прямая	от стены А, 1-й ряд вдоль неё	зазор от стены не задан
9	вдоль стен Б/Г, прямая	от стены Г, 1-й ряд вдоль неё	зазор от стены не задан
10	вдоль стен А/В, прямая	от стены А, 1-й ряд вдоль неё	зазор от стены не задан
11	вдоль стен А/В, прямая	от стены А, 1-й ряд вдоль неё	зазор от стены не задан
12	вдоль стен А/В, прямая	от стены В, 1-й ряд вдоль неё	зазор от стены не задан
13	прямая, сетка 600×600, шов 2	ось X 1216 от Г; ось Y 1046 от А	X 312 / 312; Y 443 / 443

Спецификация плинтусов

Наименование	Помещения	Длина, м (с запасом)
Плинтус МДФ под покраску 80×16, крепление к стене, окраска в цвет Tikkurila G503	6, 10, 11	38
SX165, h = 69 мм, крепление к стене, окраска в цвет Tikkurila G503	7, 12	28
Плинтус МДФ под покраску 80×16, крепление к стене, окраска в цвет Little Greene No. 222	8	9
SX165, h = 69 мм, крепление к стене, окраска в цвет NCS S 0300-N	9	9

Примечания

1. За отметку ±0,000 принят чистый пол 1-го этажа, не существующий; чистый пол этажа +3,230 (блок отметок). Площади — по чистым размерам помещений, м²; размеры — в мм.
2. Стык разнотипных покрытий — по оси дверного полотна (под полотном в закрытом положении); решение стыка — по ведомости стыков.
3. Пол санузлов ниже смежных помещений на 15 мм за счёт меньшей толщины стяжки (верх плиты общий — по экспликации полов); гидроизоляция по стяжке с заведением на стены не менее 200 мм (СП 29.13330.2011, п. 7.2), до облицовки — тест проливом и акт скрытых работ.
4. Трубопроводы в конструкции пола не прокладываются: пирог пола 49–64 мм не вмещает выпуски канализации с уклоном — выпуски К1 ведутся по стенам над чистым полом в коробах.
5. Штучные покрытия (инженерная доска): направление — по стрелке; влажность основания по СМ не более 2,0 % (по ТУ изготовителя).
6. Ровность основания — просвет под 2-метровой рейкой не более 2 мм: пом. 6, 7, 8, 9, 10, 11, 12 (инженерная доска), пом. 13 (керамогранит); проверить до укладки покрытия (СП 71.13330.2017, табл. 8.5).
7. Сетка на плитке — условная, в размер формата; точка старта и раскладка — по листу раскладки плитки.
8. Узор покрытия (заливка-код типа пола) прерывается под надписями — площадями помещений и отметками чистого пола.
9. Пироги полов — по экспликации полов: слои сверху вниз, толщины в мм; гидроизоляция мокрых зон — в пироге и в ведомости отделки; схема пола — без масштаба.


	Лист	№ док.	Подпись	Дата
Дизайнер	Кырлан А.С.			04.11.26

Проект: Дом 120 м² — **М 1:75**


План покрытий пола · 2-й этаж

Стадия	Лист	Листов
П	66	136

Фрагмент 1. Санузел гостевой (пом. 4). Пол 600×600, шов 2 мм, М 1:25

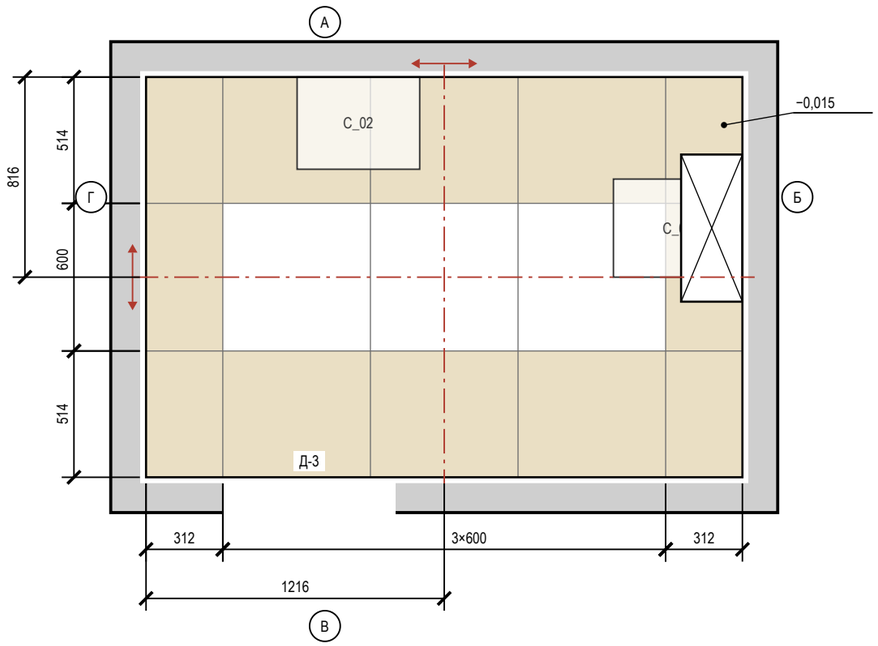

Фрагмент 2. Санузел второго этажа (пом. 13). Пол 600×600, шов 2 мм, М 1:25

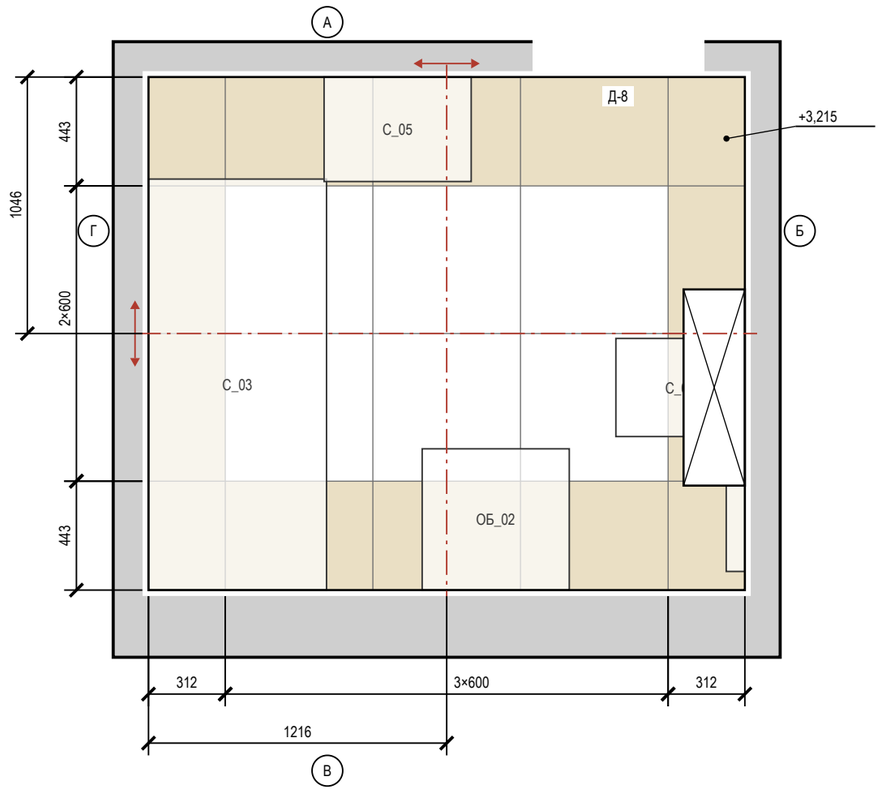

Примечания

1. Раскладка от чистовых размеров: стены санузлов теряют 10 + 5 + 9 = 24 мм на сторону (штукатурка, клей, плитка); подрезки чистые, без шва.
2. Старт — от центра помещения (штрихпунктир, стрелки направление укладки); размер старта — от чистовых стен Г и А.
3. Раскладка пола «Прихожая» и фартука «Гостиная-кухня» и фартука «Гостиная-кухня» — на листе «Раскладка плитки. Прихожая. Фартук кухни».
4. Калибр партии не задан — до укладки замерить (рабочий размер W, ГОСТ 13996-2019) и пересчитать подрезки.
5. Количество: целые по раскладке + по одной на подрезку, запас 10 %; один артикул — одна партия и тон. Исключены поддон, короб, проёмы и места за коробом; S — по чистым граням: стены нетто = зона облицовки по ведомости отделки − место за коробом инсталляции 1,68 м² (плитку за коробом не кладут), короб отдельной строкой.
6. Клей C2 TE S1 Ceresit CM 17; C2 TE S1 (ГОСТ Р 56387-2018), затирка CG2WA Mapei Ultracolor Plus 132; CG2WA; расход — по ТУ выбранной марки.
7. Гидроизоляция: пол и стены 200 мм от ЧП; над ванной — до 2000 и 300 мм за борт (пом. 13) (см. развёртки); акт скрытых работ, пролив 24 ч.
8. Швы пола совмещены со швами стены А; по периметру — демпферная лента.
9. Отметка чистого пола −0,015, +3,215, порог 15 мм; стык с соседним покрытием — по оси полотна двери.

Ведомость плитки

Помещение, поверхность	Плитка, код	Формат	Шов	S, м²	Целых	Подр.	С запасом
Санузел гостевой, пол	аналог: керамогранит под травертин	600×600	2	4,17	3	12	17
Санузел гостевой, стены А–Г	A8UZ	600×1200	2	16,68	11	21	36
Санузел гостевой, короб инсталляции	A8UZ	600×1200	2	1,47	1	3	5
Санузел второго этажа, пол	аналог: керамогранит под травертин	600×600	2	5,31	6	14	22
Санузел второго этажа, стены А–Г	A8UZ	600×1200	2	18,10	16	19	39
Санузел второго этажа, короб инсталляции	A8UZ	600×1200	2	1,76	0	6	7
Прихожая, пол	A8UZ	600×1200	2	12,20	4	22	29
Гостиная-кухня, фартук (ст. А)	аналог: керамогранит под травертин, матовый	1200×600	2	0,89	0	3	4
Гостиная-кухня, фартук (ст. Б)	аналог: керамогранит под травертин, матовый	1200×600	2	1,05	0	4	5
Итого 600×600				9,48	9	26	39
Итого 600×1200				**52,15**	**32**	**78**	**125**

Ведомость материалов


Материал	Класс, код	Норма расхода	Кол-во
Затирка	CG2WA Mapei Ultracolor Plus 132	(a+b)/ab·шов·t·1,6	4,1 кг
Затирка	CG2WA	(a+b)/ab·шов·t·1,6	1,1 кг
Клей	C2 TE S1 Ceresit CM 17	1,5 кг/м²·мм, слой 5	402 кг (17 меш.)
Клей	C2 TE S1	1,5 кг/м²·мм, слой 5	115 кг (5 меш.)
Гидроизоляция	обмазочная, 2 слоя: пол, стены по периметру и зоны замачивания	по ТУ	19,6 м²
Демпф. лента	по периметру пола из плитки		33,3 м

Условные обозначения


- плитка целая; тонкая линия — шов
- плитка с подрезкой (размер — на цепочке)
- ось старта; стрелки — направление укладки
- сантехприбор: габарит, высота по практике
- короб инсталляции: плитка пола — до короба
- отметка чистого пола на полке выноски, м
- (А) обозначение стены А–Г (как на развёртках)

					Проект: Дом 120 м²	**М 1:25**
	Лист	№ док.	Подпись	Дата		
Дизайнер	Кырлан А.С.			04.11.26	Раскладка плитки. Планы полов	Стадия: П; Лист: 67; Листов: 136


Фрагмент 1. Прихожая (пом. 5). Пол 600×1200, шов 2 мм, М 1:40

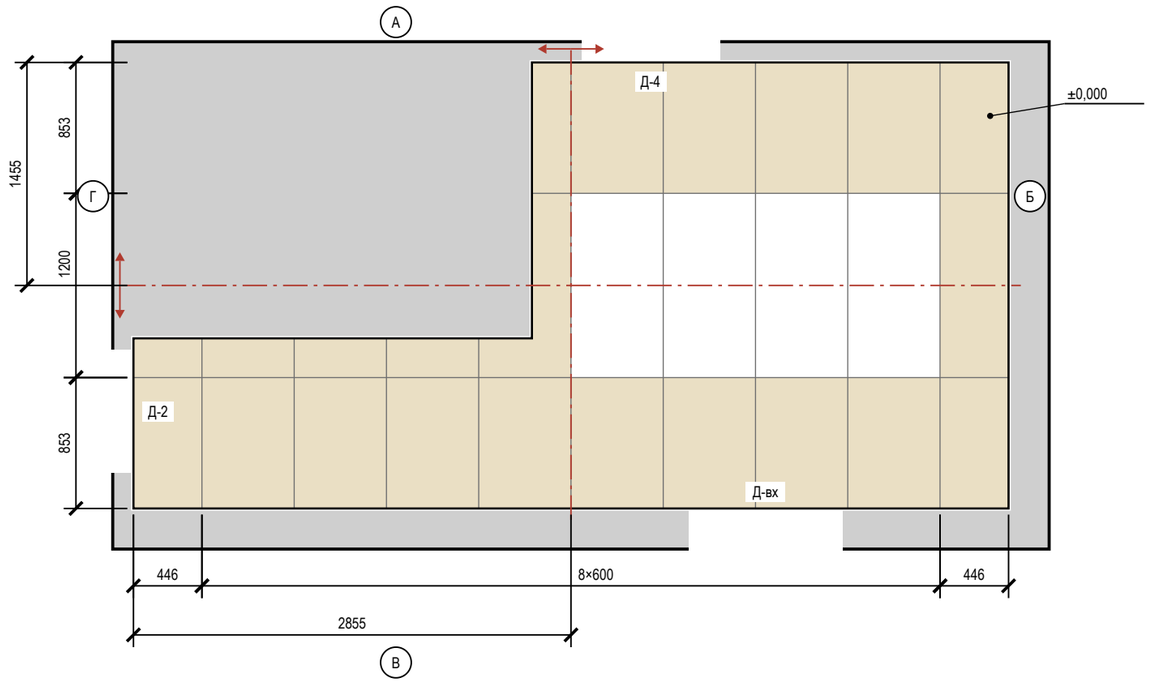

Фрагмент 2. Гостиная-кухня (пом. 1), фартук, стена А. 1200×600, шов 2 мм, М 1:40

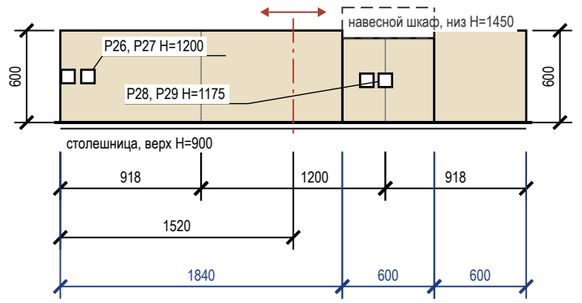

Фрагмент 3. Гостиная-кухня (пом. 1), фартук, стена Б. 1200×600, шов 2 мм, М 1:40

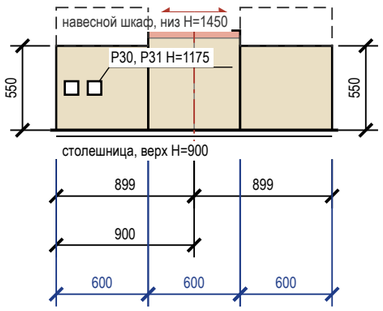

Условные обозначения

- плитка целая; тонкая линия — шов
- плитка с подрезкой (размер — на цепочке)
- ось старта; стрелки — направление укладки
- электроточка: марка и H — по листам ЭОМ
- столешница (верх)
- навесной шкаф над фартуком
- отметка чистого пола на полке выноски, м
- (А) обозначение стены А–Г (как на развёртках)

Подсчёт плитки

Поверхность	Формат	S, м²	Целых	Подр.	С запасом
Прихожая, пол	600×1200	12,20	4	22	29
Гостиная-кухня, фартук (ст. А)	1200×600	0,89	0	3	4
Гостиная-кухня, фартук (ст. Б)	1200×600	1,05	0	4	5

Примечания

1. Прихожая: керамогранит 600×1200, длинная сторона — вдоль стен Б и Г, шов 2 мм, прямая раскладка от центра. Стены окрашены: раскладка от чистового контура минус штукатурка и шпаклёвка 15 мм на сторону (принято); подрезки 446 / 853 мм, срез — под плинтус.
2. Прихожая: деформационный зазор по периметру 8–10 мм под плинтусом; в проёмах — стык с соседним покрытием по оси полотна двери. Клей C2 TE S1, затирка CG2WA.
3. Фартук, Гостиная-кухня: 1200×600 горизонтально, шов 2 мм; зоны 1840 мм — 900…1500, 600 мм — 900…1450, 600 мм — 900…1500 (от столешницы до низа навесного шкафа, без шкафа — 600 мм). Старт от центра участка, подрезки 918 мм. Площадь 0,89 м² — как в ведомости отделки.
4. Фартук — после монтажа столешницы, низ на 2–3 мм выше неё, шов со столешницей — санитарный герметик; навесные шкафы — после фартука. Торцы у пенала и стены — профиль или запил 45°.
5. Фартук, Гостиная-кухня: 1200×600 горизонтально, шов 2 мм; зоны 600 мм — 900…1450, 600 мм — 900…1550, 600 мм — 900…1450 (от столешницы до низа навесного шкафа, без шкафа — 650 мм). Старт от центра участка, подрезки 899 мм. Площадь 1,05 м² — как в ведомости отделки.
6. Фартук — после монтажа столешницы, низ на 2–3 мм выше неё, шов со столешницей — санитарный герметик; навесные шкафы — после фартука. Торцы у пенала и стены — профиль или запил 45°.
7. Фартук, Гостиная-кухня: в зоне до отм. 1550 верхний ряд подрезан 48 мм — меньше 1/3 плитки; полоса прикрыта корпусом навесного модуля и на виду не остаётся. Раскладкой не снимается: убрать подрезку можно, только выровняв низ этого модуля с соседними (1450 мм) — решение мебельщика.
8. Клей, затирка и итог по форматам — в ведомостях листа «Раскладка плитки. Планы полов».

					Проект: Дом 120 м² — **М 1:40**
	Лист	№ док.	Подпись	Дата	Раскладка плитки. Прихожая. Фартук кухни
Дизайнер	Кырлан А.С.			04.11.26	Стадия: П; Лист: 68; Листов: 136

Развёртка стены А


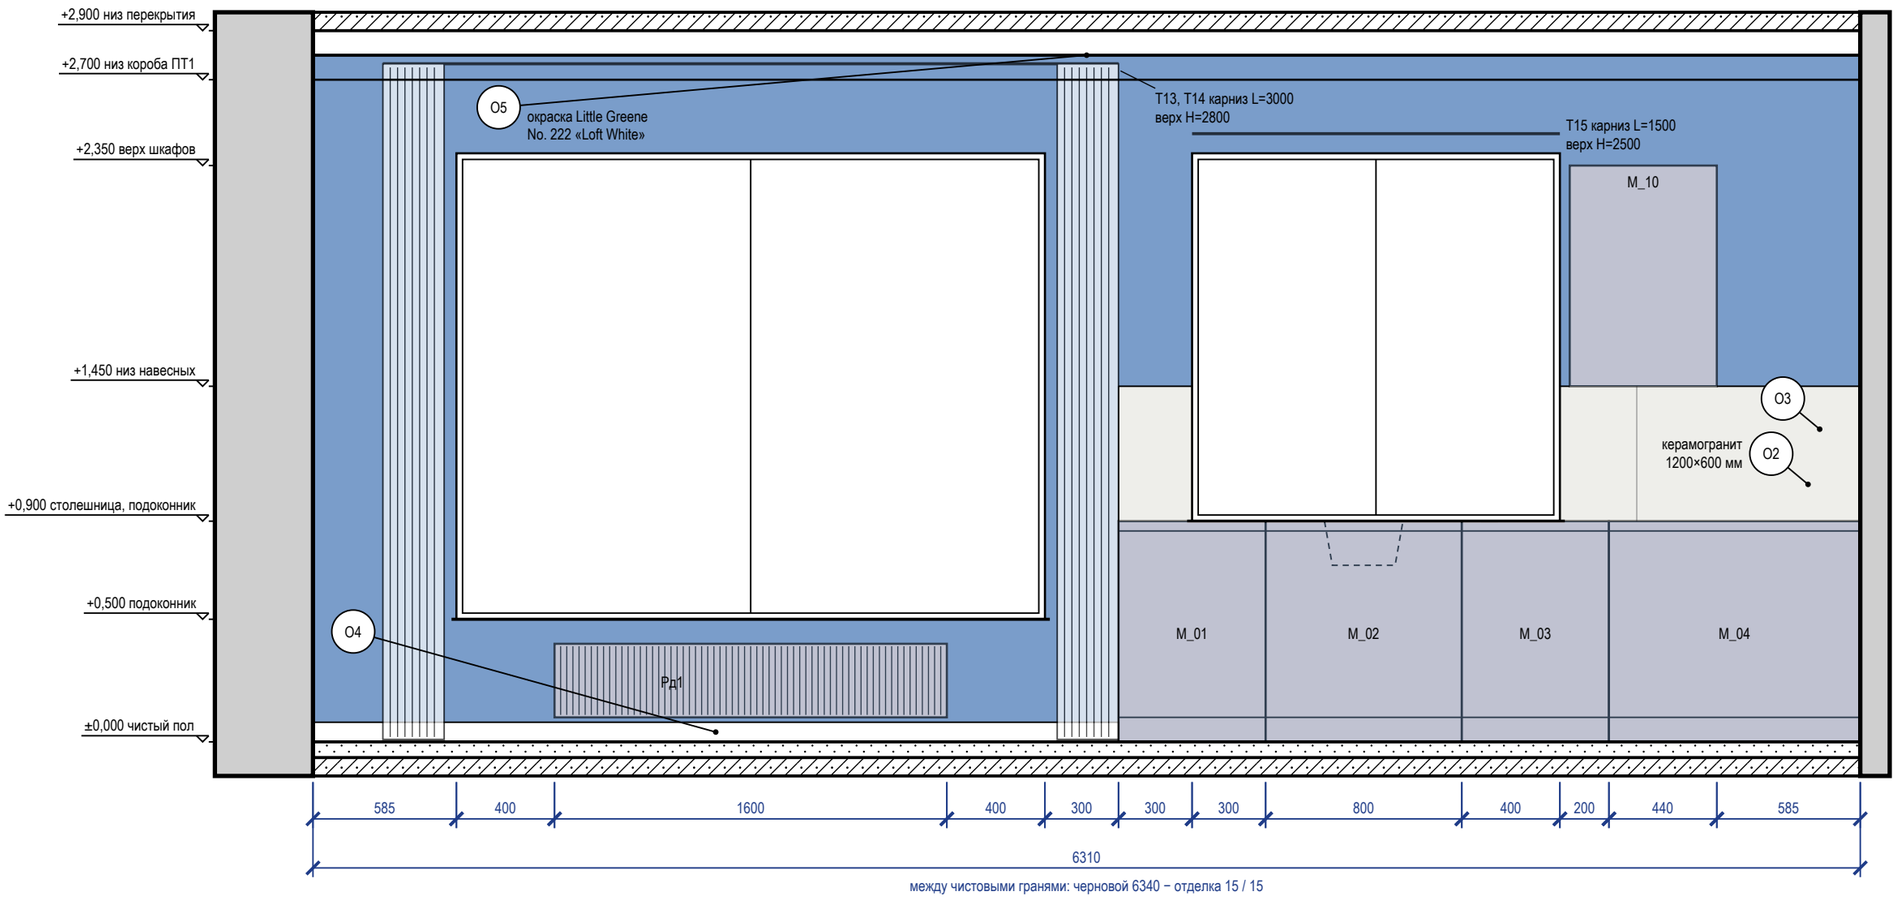


Схема развёрток (М 1:100)

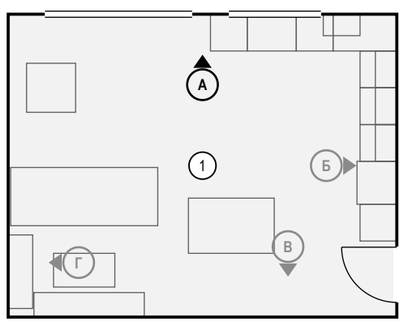

Ведомость отделки (на листе)

Марка	Поверхность	Материал, изделие	Цвет, код	Кол.
О2	фартук	керамогранит, 1200×600×9 мм, аналог: керамогранит под травертин, матовый, затирка CG2WA		0,8 м²
О3	акцентная стена	окраска, Tikkurila, матовая, подготовка Q3	NCS S 3050-R80B «Эгейский синий»	9,2 м²
О4	плинтус	плинтус МДФ, h 80 мм, аналог: плинтус МДФ под покраску 80×16	Tikkurila G503 «Calla»	3,3 м
О5	потолок	окраска, Little Greene Absolute Matt, глубокоматовая, подготовка Q3	Little Greene No. 222 «Loft White»	31,3 м²

Примечания

1. Размеры — в мм от чистовых поверхностей стен; условные обозначения и общие указания — лист 3.
2. Стена А показана двумя видами: здесь — архитектурная развёртка (мебель, отделка, проёмы, высоты), электроточки и выводы ВК с привязками и таблицей — на листе 70 («Привязки»).
3. Карнизы (шины) — по ведомости текстиля декоратора: длина L и верх H на развёртке — те же числа, что в ведомости; крепление — до окраски потолка.
4. Потолок — у каждой стены свой, по плану потолков (НШ1, ПТ1); ступени — зоной, кромка короба перед нишей — тонкой линией; в поле потолка: ПТ2 +2,750, ПТ3 +2,800.

					Проект: Дом 120 м² — М 1:25
	Лист	№ док.	Подпись	Дата	Развёртка стены А. Гостиная-кухня (пом. 1), кухонный фронт
Дизайнер	Кырлан А.С.			04.11.26	Стадия: П; Лист: 69; Листов: 136

Развёртка стены А: электроточки и выводы

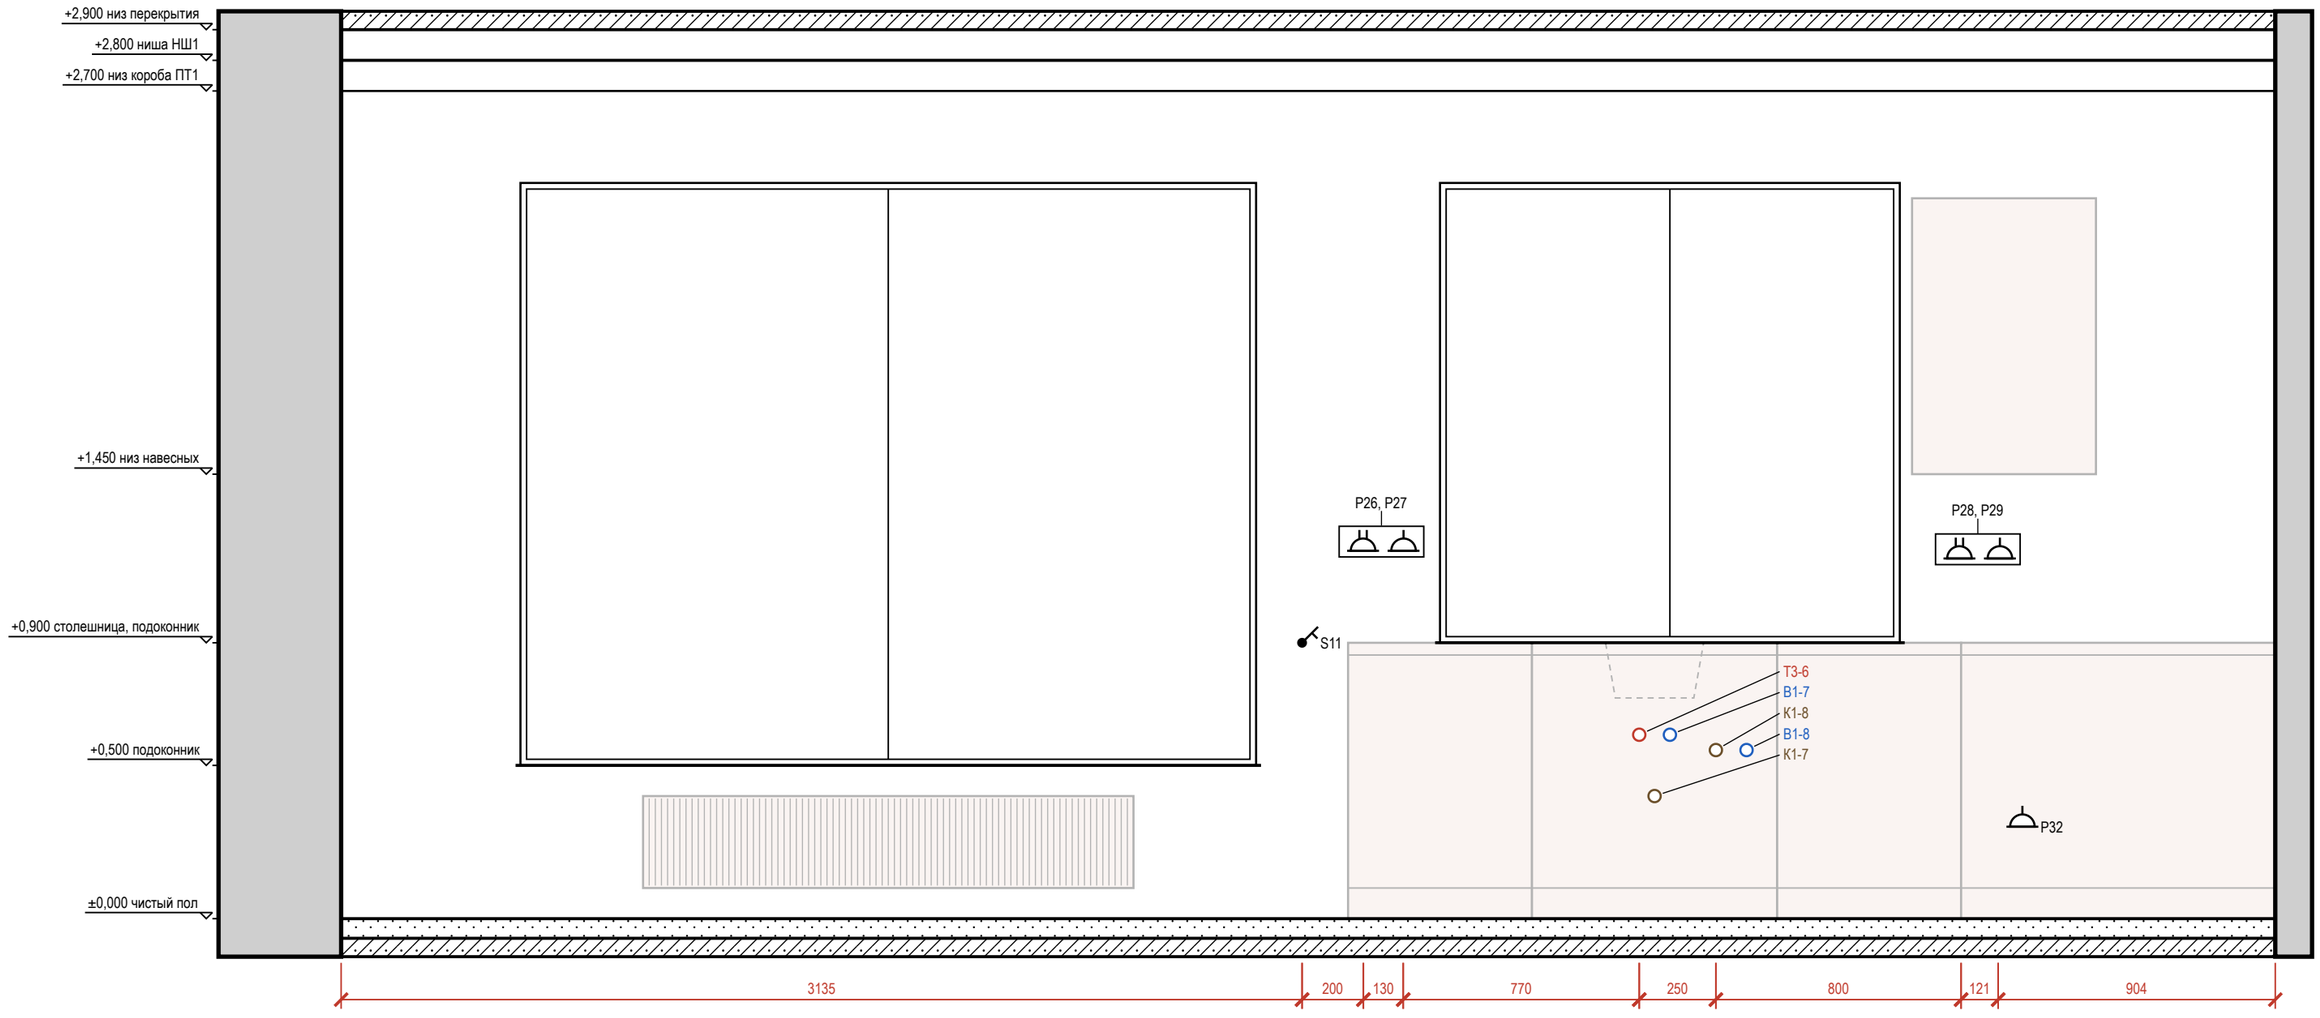


Таблица привязок электроточек и выводов

Марка	Назначение	От угла, мм	H от пола, мм	Примечание
S11	выключатель	3135	900	гр. 2
P26	розетка: фартук	3335	1200	рамка 2 поста, гр. 7
P27	розетка: фартук	3465	1200	гр. 7
T3-6	горячая вода — мойка кухонная	4235	600	межос. 100
K1-7	канализация — мойка кухонная	4285	400	Ø50
B1-7	холодная вода — мойка кухонная	4335	600	межос. 100

Марка	Назначение	От угла, мм	H от пола, мм	Примечание
K1-8	канализация — посудомоечная машина	4485	550	Ø40; слив ПММ в шкафу мойки
B1-8	холодная вода — посудомоечная машина	4585	550	кран ПММ в шкафу мойки
P28	розетка: фартук	5285	1175	рамка 2 поста, гр. 7
P29	розетка: фартук	5406	1175	гр. 7
P32	розетка: посудомоечная машина	5485	300	гр. 10

Условные обозначения

- розетка с заземляющим контактом; у знака — марка, ×N постов в рамке, гр. — группа щита, H — высота оси, мм
- выключатель одноклавишный
- вывод B1 (код — в ведомости привязок)
- вывод T3 (код — в ведомости привязок)
- вывод K1 (код — в ведомости привязок)
- привязки точек и выводов от угла и от пола, мм

Примечания

1. Вид «Привязки» стены А — электроточки и выводы ВК; архитектурная развёртка (мебель, отделка, проёмы, высоты) — на листе 69. Мебель и приборы — подложкой для ориентира; их марки и обозначения мебели, проёмов и стен — там же.
2. Привязки — в мм: по горизонтали от левого чистового угла стены до оси изделия, H — от чистого пола до оси; все точки — в таблице привязок. Красная цепочка — привязки по осям; точки ближе 120 мм одна к другой в цепочку не дробятся — их привязки только в таблице.
3. У знака — марка электроточки (P — розетка, S — выключатель, Св — светильник, ЭВ — вывод кабеля); условные обозначения и общие указания — лист 3.
4. Коды выводов ВК: B1 — холодная вода, T3 — горячая вода, K1 — канализация; номер после дефиса — номер вывода на листе выводов сантехники.
5. Выводы кухонной техники — по утверждённому проекту кухни: привязки выводов даются от осей модулей гарнитура.

					Проект: Дом 120 м²	**М 1:20**
	Лист	№ док.	Подпись	Дата	Привязки электроточек и выводов ВК, стена А. Гостиная-кухня (пом. 1)	
Дизайнер	Кырлан А.С.			04.11.26		
					Стадия: П	Лист: 70 / Листов: 136

Развёртка стены Б


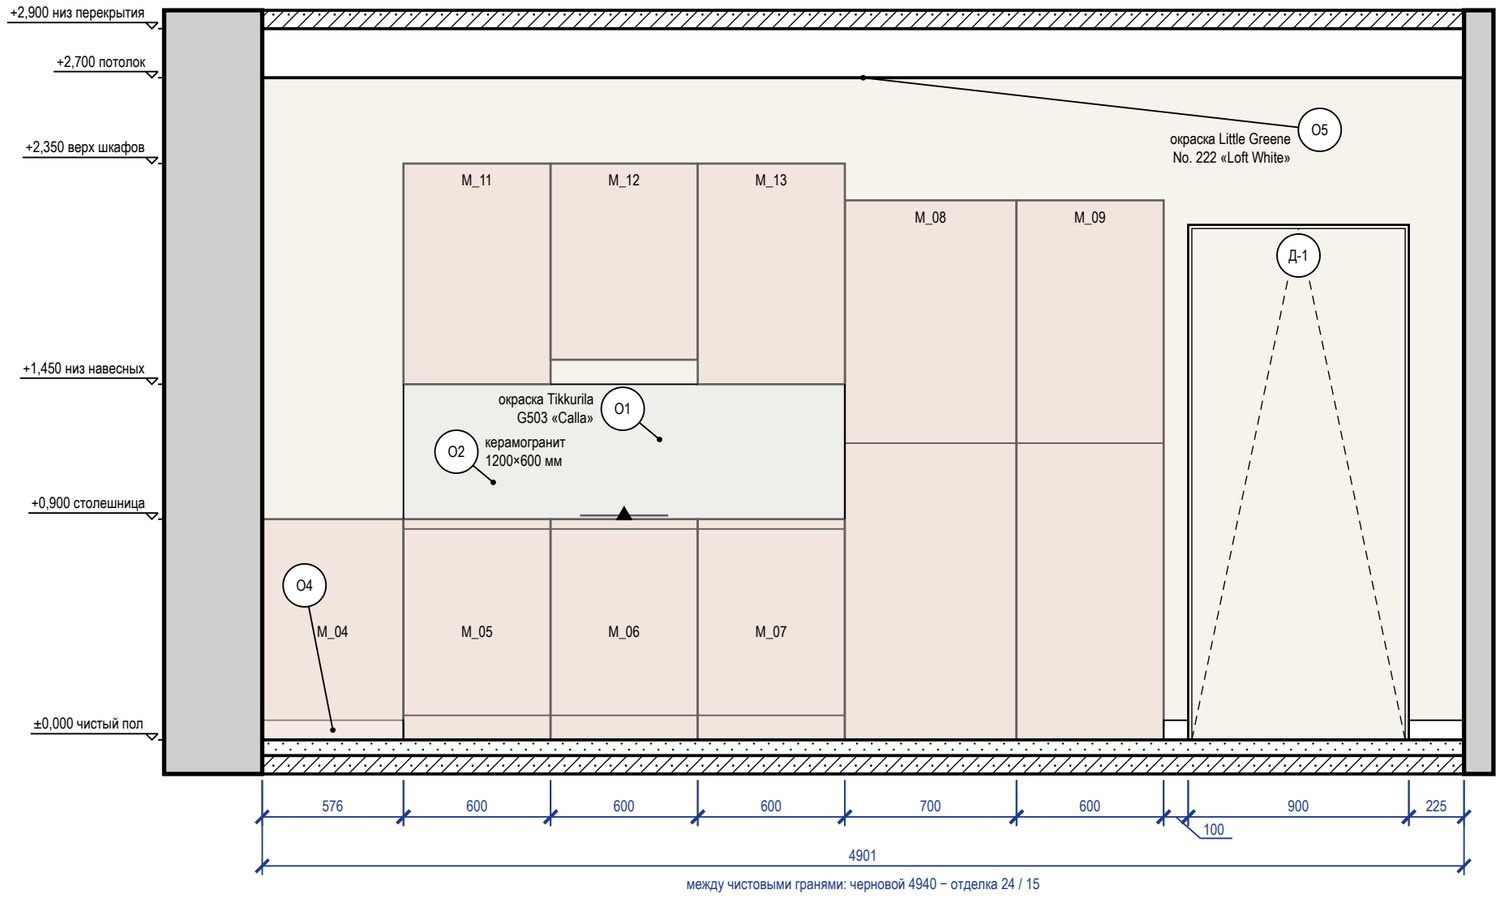


Схема развёрток (М 1:100)

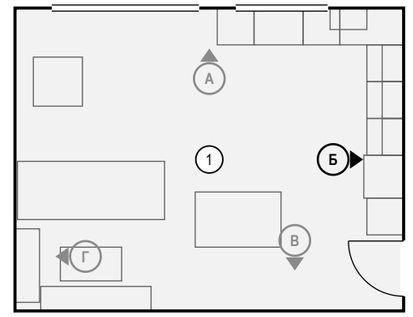

Ведомость отделки (на листе)

Марка	Поверхность	Материал, изделие	Цвет, код	Кол.
О1	стены	окраска, Tikkurila, матовая, подготовка Q3	Tikkurila G503 «Calla»	10,4 м²
О2	фартук	керамогранит, 1200×600×9 мм, аналог: керамогранит под травертин, матовый, затирка CG2WA		1 м²
О4	плинтус	плинтус МДФ, h 80 мм, аналог: плинтус МДФ под покраску 80×16	Tikkurila G503 «Calla»	0,9 м
О5	потолок	окраска, Little Greene Absolute Matt, глубокоматовая, подготовка Q3	Little Greene No. 222 «Loft White»	31,3 м²

Примечания

1. Размеры — в мм от чистовых поверхностей стен; условные обозначения и общие указания — лист 3.
2. Стена Б показана двумя видами: здесь — архитектурная развёртка (мебель, отделка, проёмы, высоты), электроточки и выводы ВК с привязками и таблицей — на листе 72 («Привязки»).
3. Двери скрытого монтажа — полотно в плоскости стены, отделка стены по полотну, плинтус прерывается у короба (узел — на листе узлов).
4. Потолок — у каждой стены свой, по плану потолков (ПТ1); ступени — зоной, кромка короба перед нишей — тонкой линией; в поле потолка: ПТ2 +2,750, ПТ3 +2,800.

	Лист	№ док.	Подпись	Дата
Дизайнер	Кырлан А.С.			04.11.26

Проект: Дом 120 м² — **М 1:25**

Развёртка стены Б. Гостиная-кухня (пом. 1), кухонный фронт	Стадия	Лист	Листов
	П	71	136

Развёртка стены Б: электроточки и выводы

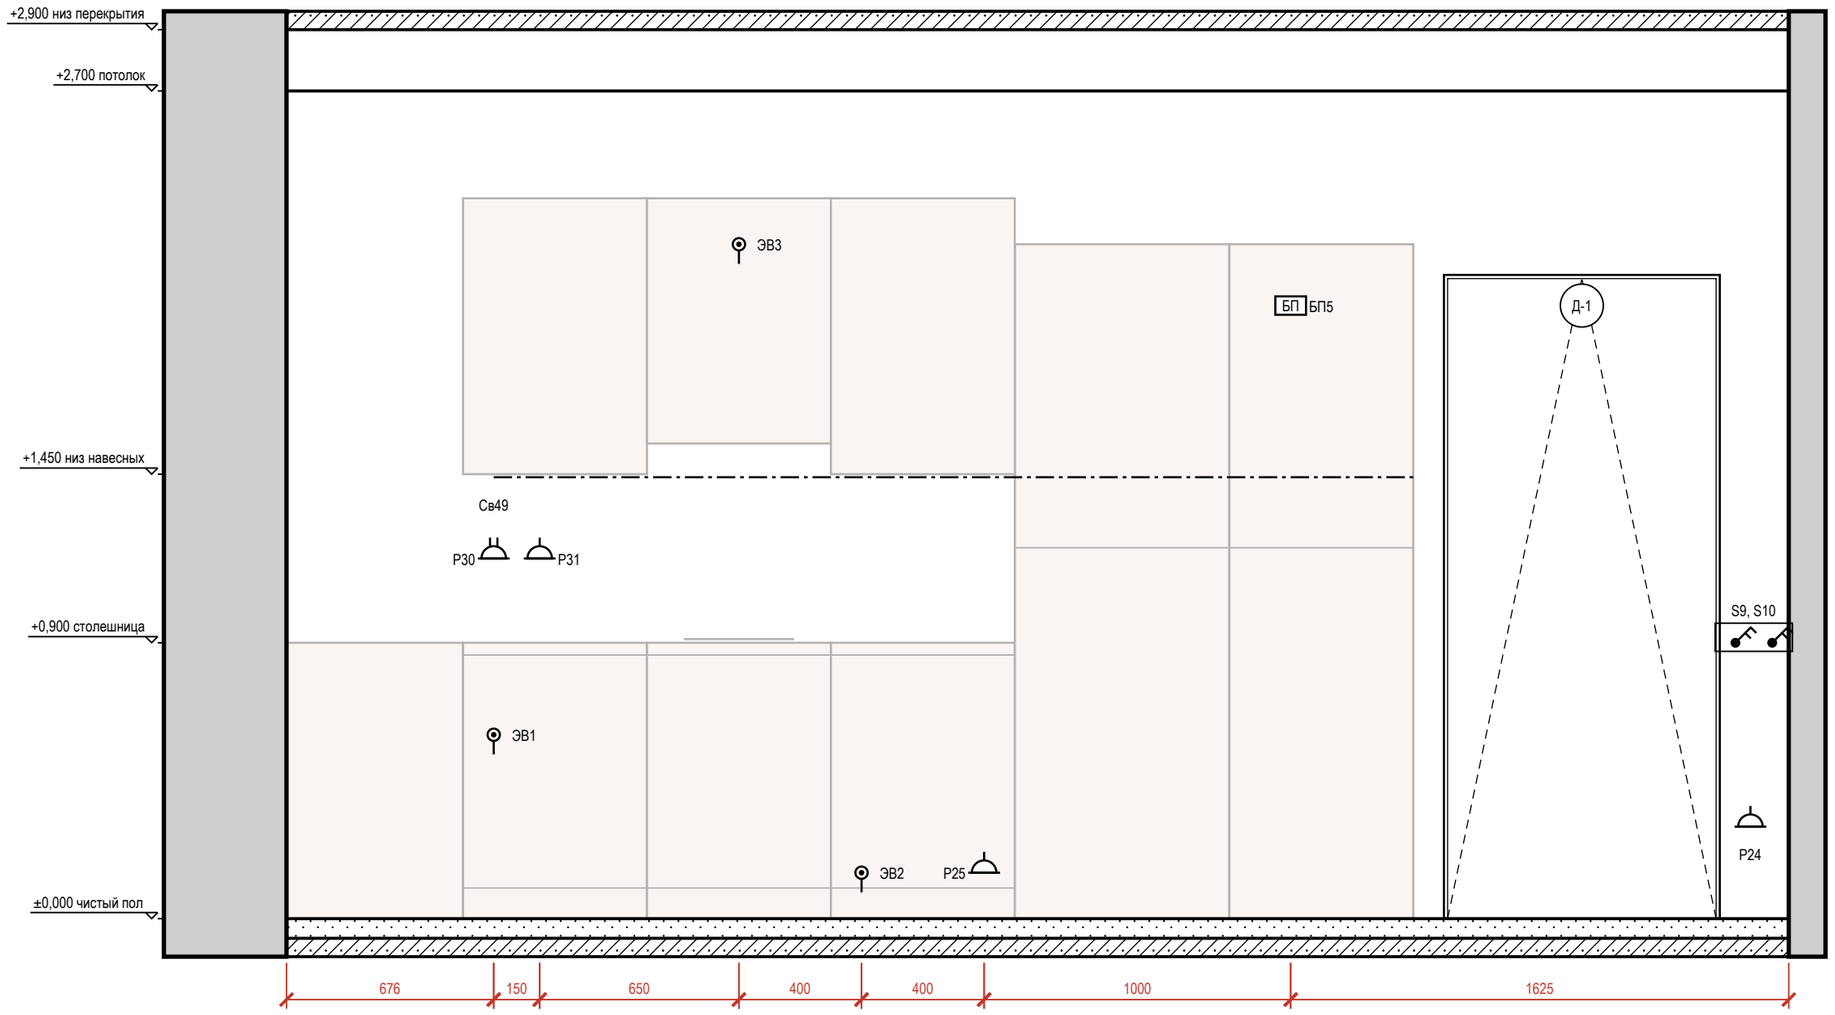


Таблица привязок электроточек и выводов

Марка	Назначение	От угла, мм	Н от пола, мм	Примечание
ЭВ1	вывод кабеля: варочная панель M_06 (вывод в соседнем модуле M_05, за ящиком)	676	600	гр. 8
Р30	розетка: фартук между мойкой и варочной	676	1175	рамка 2 поста, гр. 7
Св49	светильник настенный	676	1440	гр. 2, лента 676–3676 от угла
Р31	розетка: фартук между мойкой и варочной	826	1175	гр. 7
ЭВ3	вывод кабеля: вытяжка	1476	2200	гр. 11
ЭВ2	вывод кабеля: духовой шкаф	1876	150	гр. 9

Марка	Назначение	От угла, мм	Н от пола, мм	Примечание
Р25	розетка: холодильник M_08 (розетка в соседнем модуле M_07, съёмная панель)	2276	150	гр. 11
БП5	блок питания LED: в пенале M_09, верх, съёмная панель	3276	2000	гр. 2
Р24	розетка: у обеденного стола	4776	300	гр. 6
S9	выключатель	4776	900	гр. 2
S10	выключатель	4856	900	рамка 2 поста, гр. 2

Условные обозначения

- розетка с заземляющим контактом; у знака — марка, ×N постов в рамке, гр. — группа щита, Н — высота оси, мм
- вывод кабеля для подключения прибора (без розетки), марка ЭВ
- выключатель одноклавишный
- выключатель двухклавишный (флажков — по числу клавиш)
- светодиодная лента в профиле / в карнизе короба
- БП — блок питания LED, с доступом (люк от 100×100 мм)
- привязки точек и выводов от угла и от пола, мм

Примечания

1. Вид «Привязки» стены Б — электроточки и выводы ВК; архитектурная развёртка (мебель, отделка, проёмы, высоты) — на листе 71. Мебель и приборы — подложкой для ориентира; их марки и обозначения мебели, проёмов и стен — там же.
2. Привязки — в мм: по горизонтали от левого чистового угла стены до оси изделия, Н — от чистого пола до оси; все точки — в таблице привязок. Красная цепочка — привязки по осям; точки ближе 120 мм одна к другой в цепочку не дробятся — их привязки только в таблице.
3. У знака — марка электроточки (Р — розетка, S — выключатель, Св — светильник, ЭВ — вывод кабеля); условные обозначения и общие указания — лист 3.
4. Выводы кухонной техники — по утверждённому проекту кухни: привязки выводов даются от осей модулей гарнитура.

					Проект: Дом 120 м² — М 1:20
	Лист	№ док.	Подпись	Дата	Привязки электроточек, стена Б. Гостиная-кухня (пом. 1)
Дизайнер	Кырлан А.С.			04.11.26	Стадия: П; Лист: 72; Листов: 136

Развёртка стены В


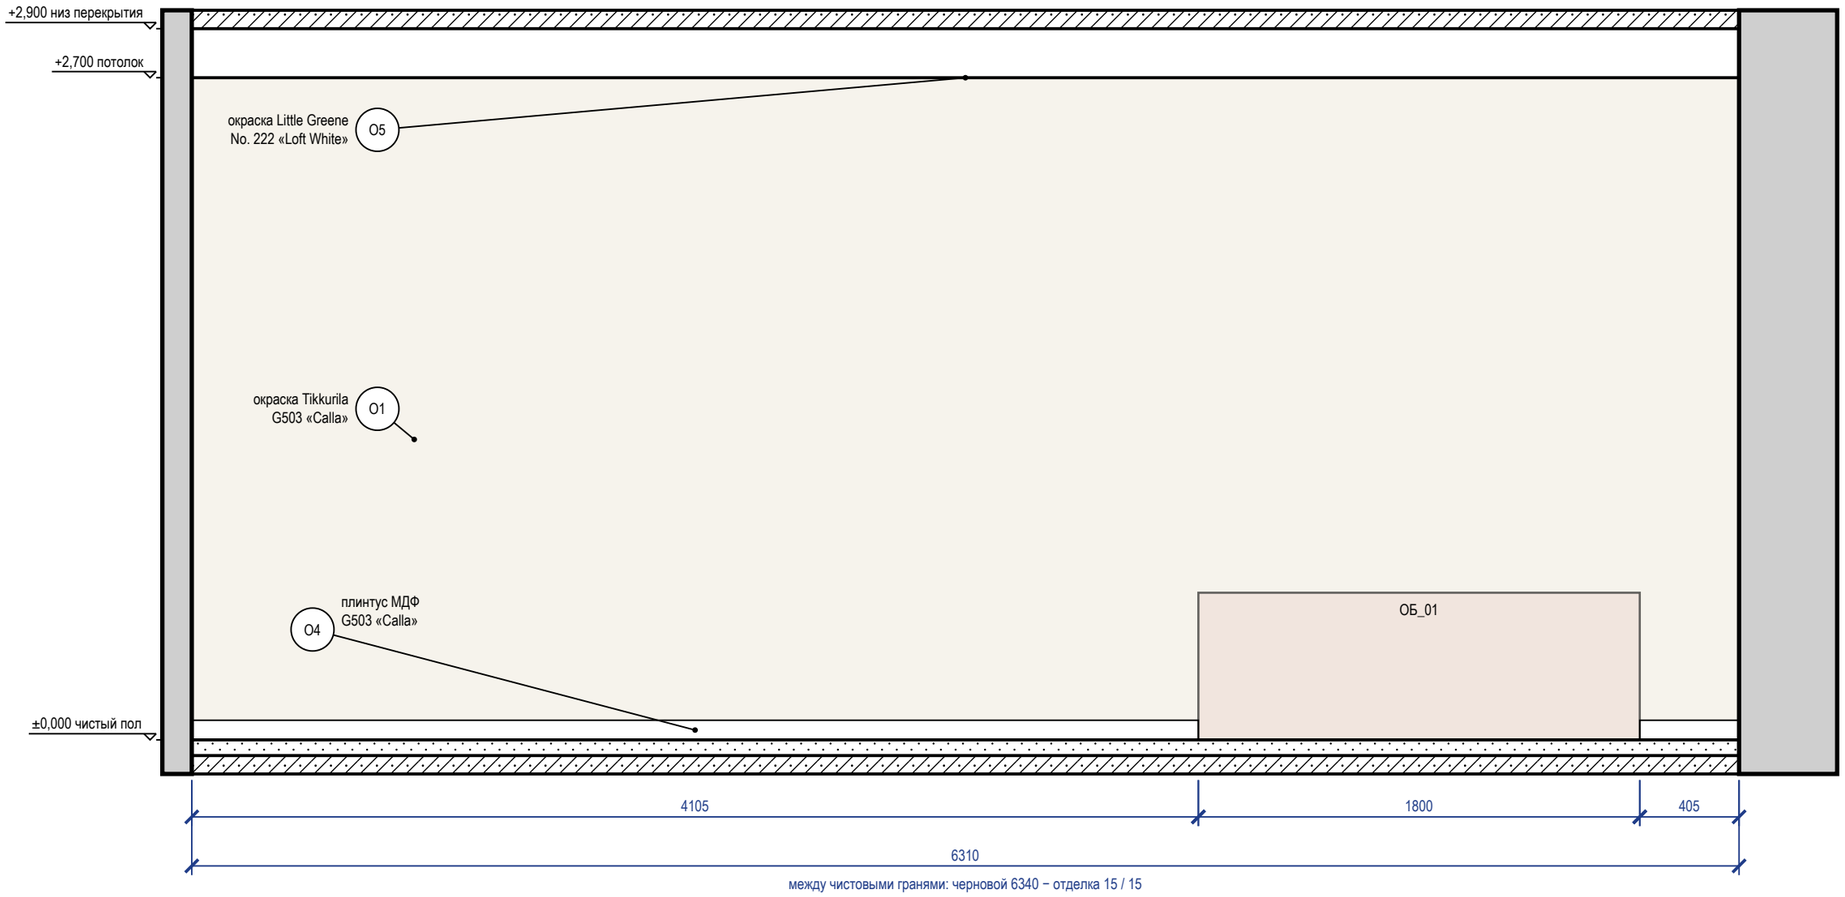


Схема развёрток (М 1:100)

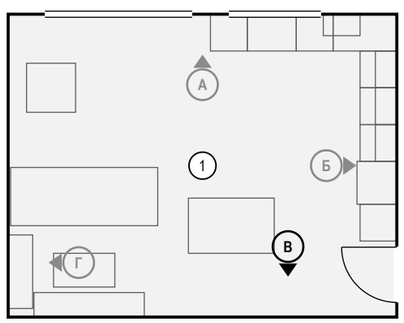

Ведомость отделки (на листе)

Марка	Поверхность	Материал, изделие	Цвет, код	Кол.
О1	стены	окраска, Tikkurila, матовая, подготовка Q3	Tikkurila G503 «Calla»	17 м²
О4	плинтус	плинтус МДФ, h 80 мм, аналог: плинтус МДФ под покраску 80×16	Tikkurila G503 «Calla»	4,5 м
О5	потолок	окраска, Little Greene Absolute Matt, глубокоматовая, подготовка Q3	Little Greene No. 222 «Loft White»	31,3 м²

Примечания

1. Размеры — в мм от чистовых поверхностей стен; условные обозначения и общие указания — лист 3.
2. Стена В показана двумя видами: здесь — архитектурная развёртка (мебель, отделка, проёмы, высоты), электроточки и выводы ВК с привязками и таблицей — на листе 74 («Привязки»).
3. Потолок — у каждой стены свой, по плану потолков (ПТ1); ступени — зоной, кромка короба перед нишей — тонкой линией; в поле потолка: ПТ2 +2,750, ПТ3 +2,800.

					Проект: Дом 120 м²	М 1:25
	Лист	№ док.	Подпись	Дата	Развёртка стены В. Гостиная-кухня (пом. 1)	Стадия / Лист / Листов
Дизайнер	Кырлан А.С.			04.11.26		П / 73 / 136

Развёртка стены В: электроточки и выводы

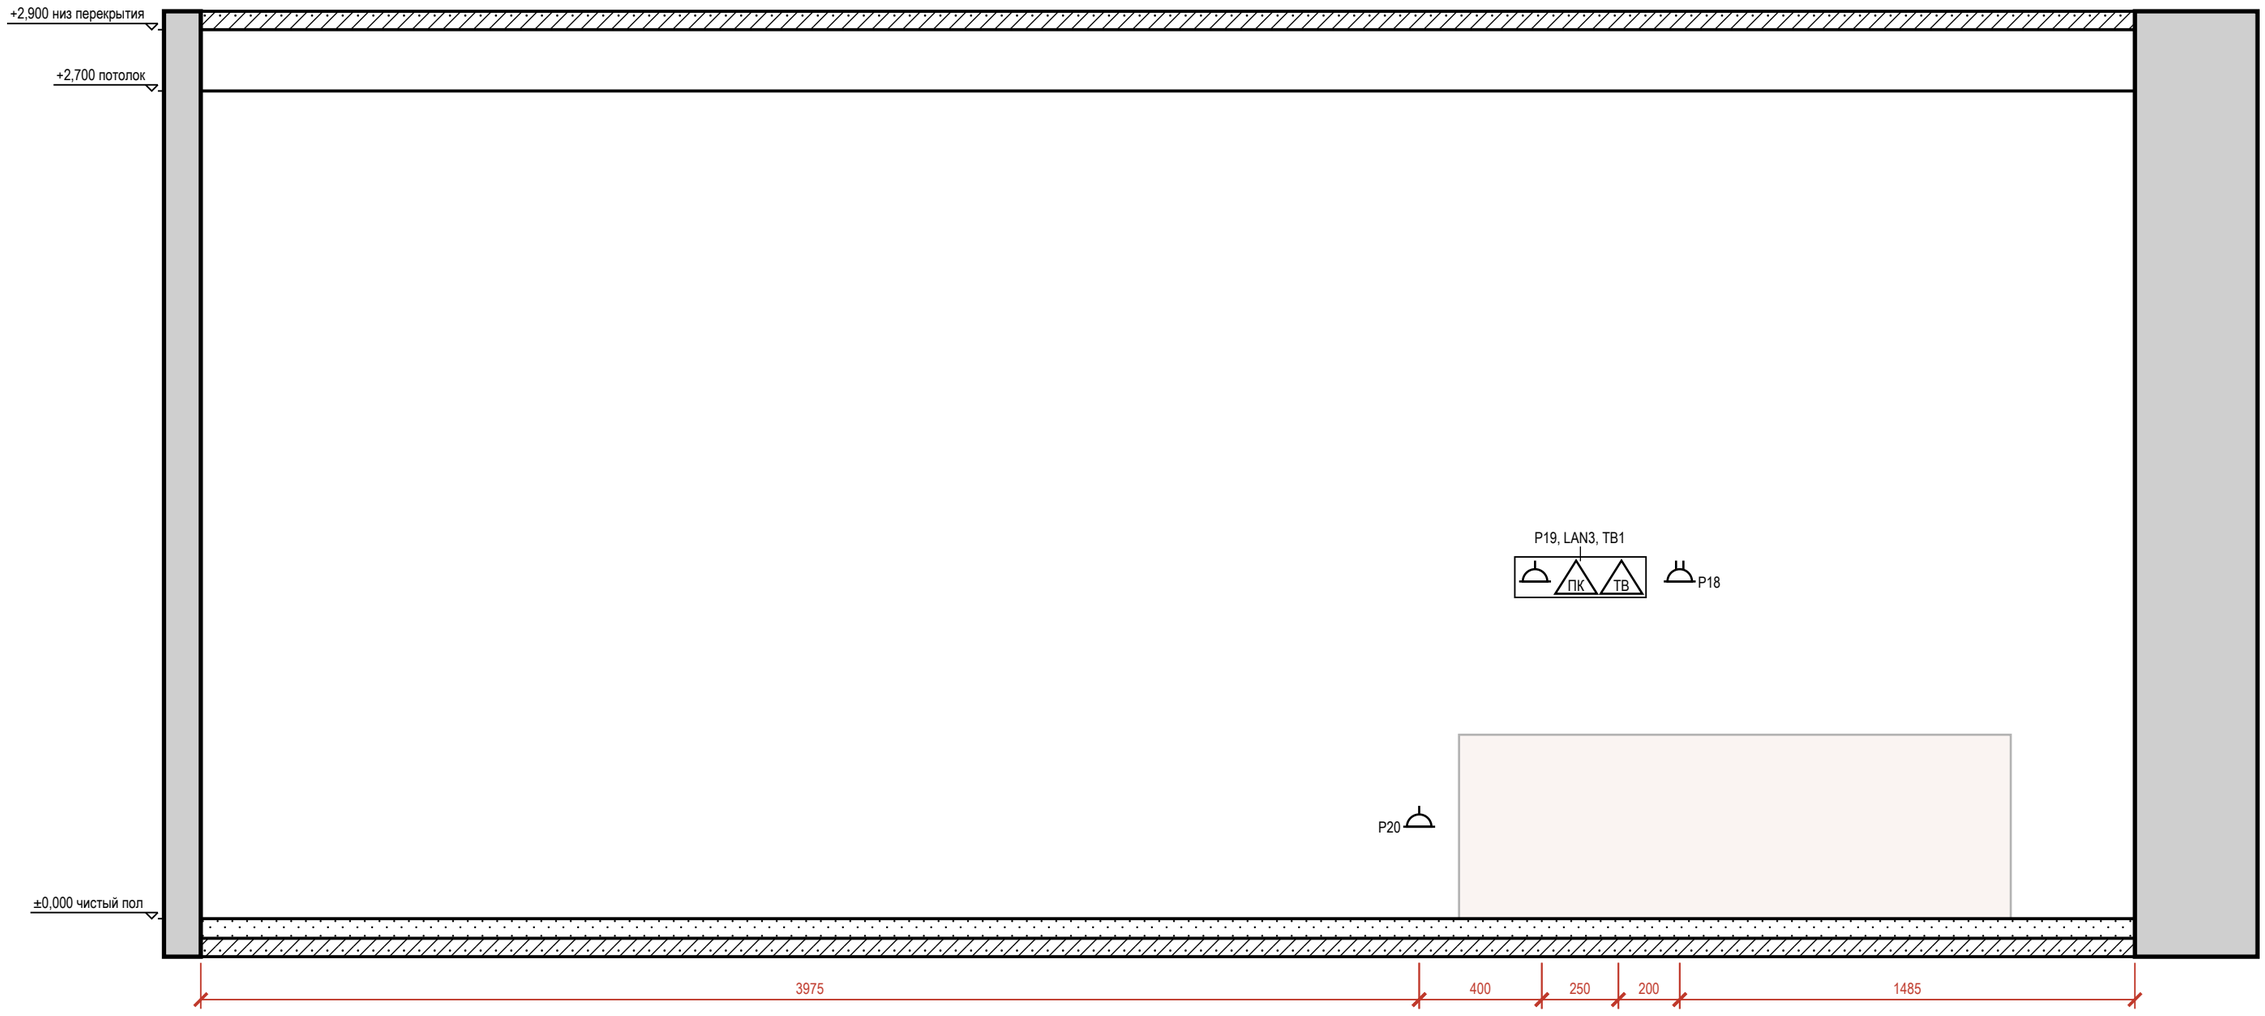



Таблица привязок электроточек и выводов

Марка	Назначение	От угла, мм	H от пола, мм	Примечание
P20	розетка: у ТВ-тумбы	3975	300	гр. 6
P19	розетка: ТВ-приставка (в одной зоне с TB1, LAN3)	4375	1100	гр. 6
LAN3	розетка RJ45: Smart TV	4475	1100	
TB1	розетка ТВ: ТВ-зона	4625	1100	
P18	розетка: ТВ (в одной зоне с TB1, LAN3)	4825	1100	рамка 2 поста, гр. 6

Условные обозначения

- розетка с заземляющим контактом; у знака — марка, ×N постов в рамке, гр. — группа щита, H — высота оси, мм
- ПК — розетка компьютерная RJ45
- ТВ — розетка телевизионная
- привязки точек и выводов от угла и от пола, мм
- A — марка развёртки: буква стены, стрелка — взгляд

Схема развёрток (М 1:200)

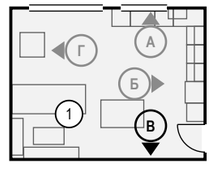

Примечания

1. Вид «Привязки» стены В — электроточки и выводы ВК; архитектурная развёртка (мебель, отделка, проёмы, высоты) — на листе 73. Мебель и приборы — подложкой для ориентира; их марки и обозначения мебели, проёмов и стен — там же.
2. Привязки — в мм: по горизонтали от левого чистового угла стены до оси изделия, H — от чистого пола до оси; все точки — в таблице привязок. Красная цепочка — привязки по осям; точки ближе 120 мм одна к другой в цепочку не дробятся — их привязки только в таблице.
3. У знака — марка электроточки (P — розетка, S — выключатель, Св — светильник, ЭВ — вывод кабеля); условные обозначения и общие указания — лист 3.


	Лист	№ док.	Подпись	Дата
Дизайнер	Кырлан А.С.			04.11.26

Проект: Дом 120 м² — М 1:20

Привязки электроточек, стена В. Гостиная-кухня (пом. 1)


Стадия	Лист	Листов
П	74	136

Развёртка стены Г

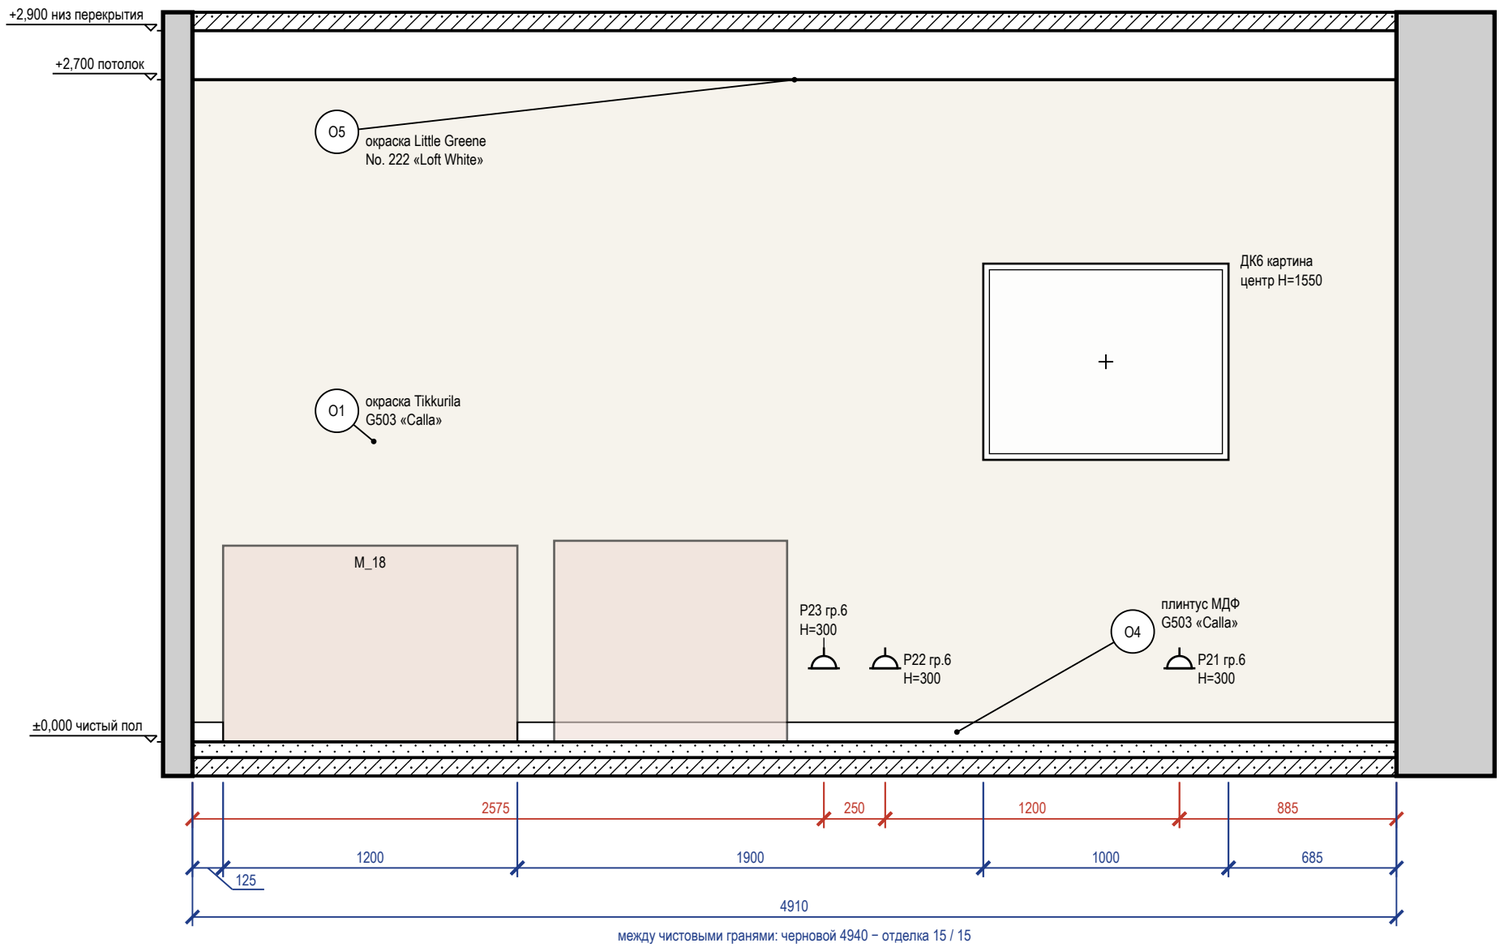

между чистовыми гранями: черновой 4940 − отделка 15 / 15

Схема развёрток (М 1:100)

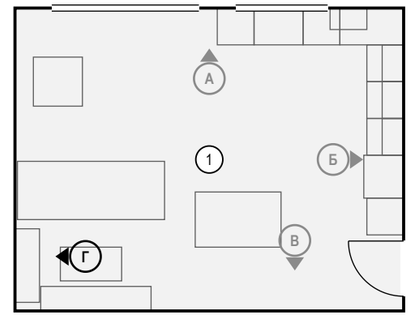

Ведомость отделки (на листе)

Марка	Поверхность	Материал, изделие	Цвет, код	Кол.
О1	стены	окраска, Tikkurila, матовая, подготовка Q3	Tikkurila G503 «Calla»	13,3 м²
О4	плинтус	плинтус МДФ, h 80 мм, аналог: плинтус МДФ под покраску 80×16	Tikkurila G503 «Calla»	3,7 м
О5	потолок	окраска, Little Greene Absolute Matt, глубокоматовая, подготовка Q3	Little Greene No. 222 «Loft White»	31,3 м²

Примечания

1. Размеры — в мм от чистовых поверхностей стен; условные обозначения и общие указания — лист 3.
2. Картины и зеркала крепить к основанию по паспорту изделия (закладные и анкеры — в перечне скрытых работ); крест — ось центра предмета.
3. Потолок — у каждой стены свой, по плану потолков (ПТ1); ступени — зоной, кромка короба перед нишей — тонкой линией; в поле потолка: ПТ2 +2,750, ПТ3 +2,800.

					Проект: Дом 120 м² — М 1:25
	Лист	№ док.	Подпись	Дата	Развёртка стены Г. Гостиная-кухня (пом. 1)
Дизайнер	Кырлан А.С.			04.11.26	

Стадия	Лист	Листов
П	75	136

Развёртка стены А


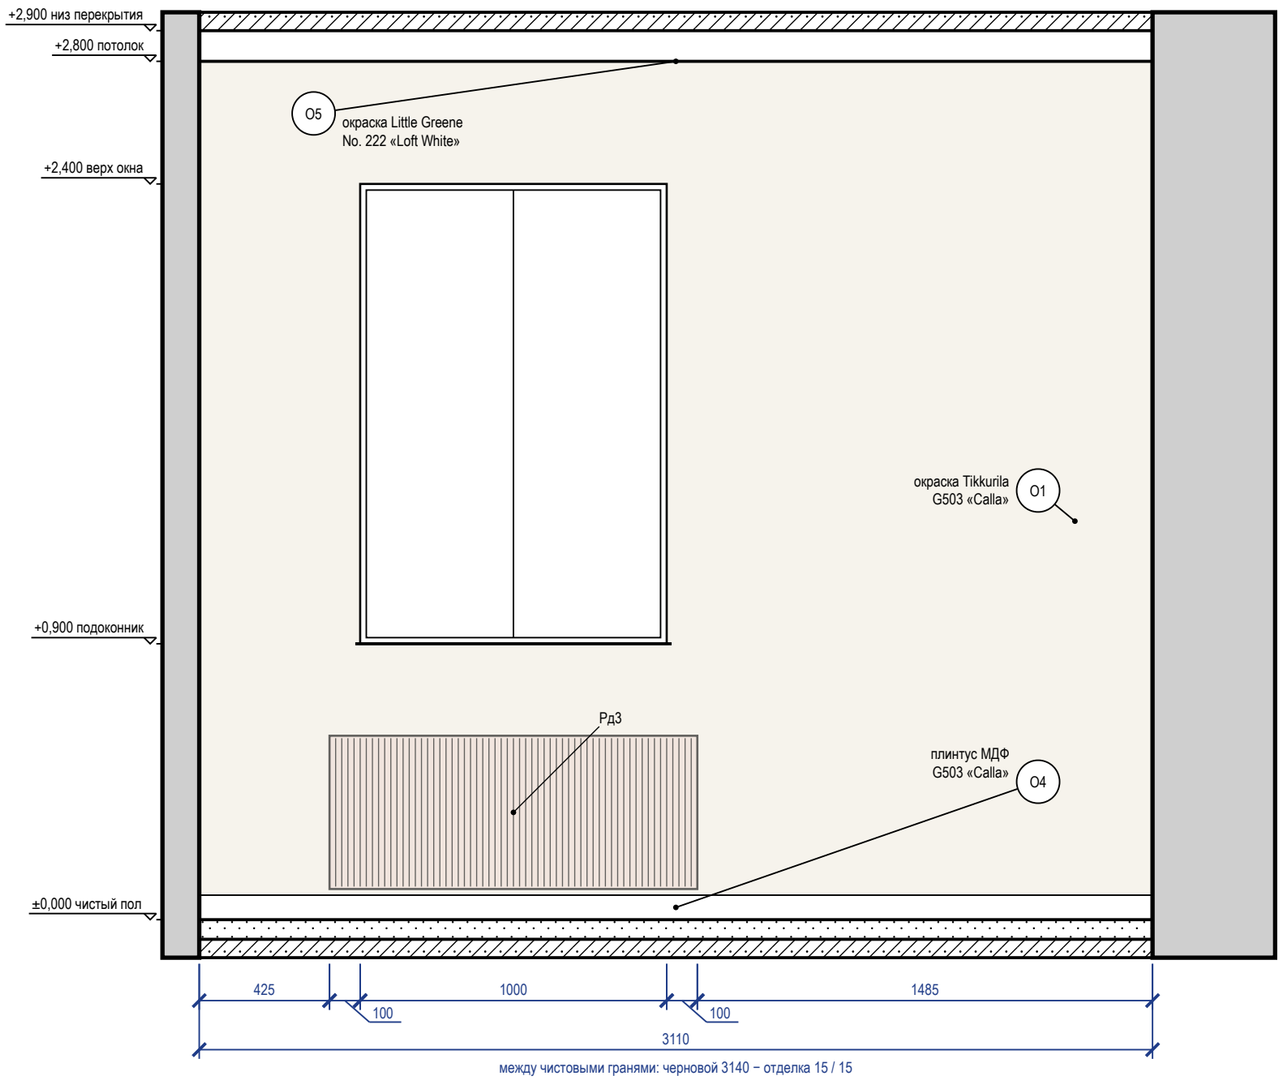


Схема развёрток (М 1:100)

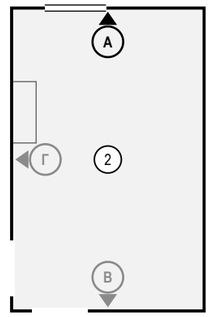

Ведомость отделки (на листе)

Марка	Поверхность	Материал, изделие	Цвет, код	Кол.
О1	стены	окраска, Tikkurila, матовая, подготовка Q3	Tikkurila G503 «Calla»	7,2 м²
О4	плинтус	плинтус МДФ, h 80 мм, аналог: плинтус МДФ под покраску 80×16	Tikkurila G503 «Calla»	3,1 м
О5	потолок	окраска, Little Greene Absolute Matt, глубокоматовая, подготовка Q3	Little Greene No. 222 «Loft White»	15,5 м²

Примечания

1. Размеры — в мм от чистовых поверхностей стен; условные обозначения и общие указания — лист 3.

					Проект: Дом 120 м²	М 1:20
	Лист	№ док.	Подпись	Дата		
Дизайнер	Кырлан А.С.			04.11.26	Развёртка стены А. Холл с лестницей (пом. 2)	Стадия: П; Лист: 76; Листов: 136

Развёртка стены В


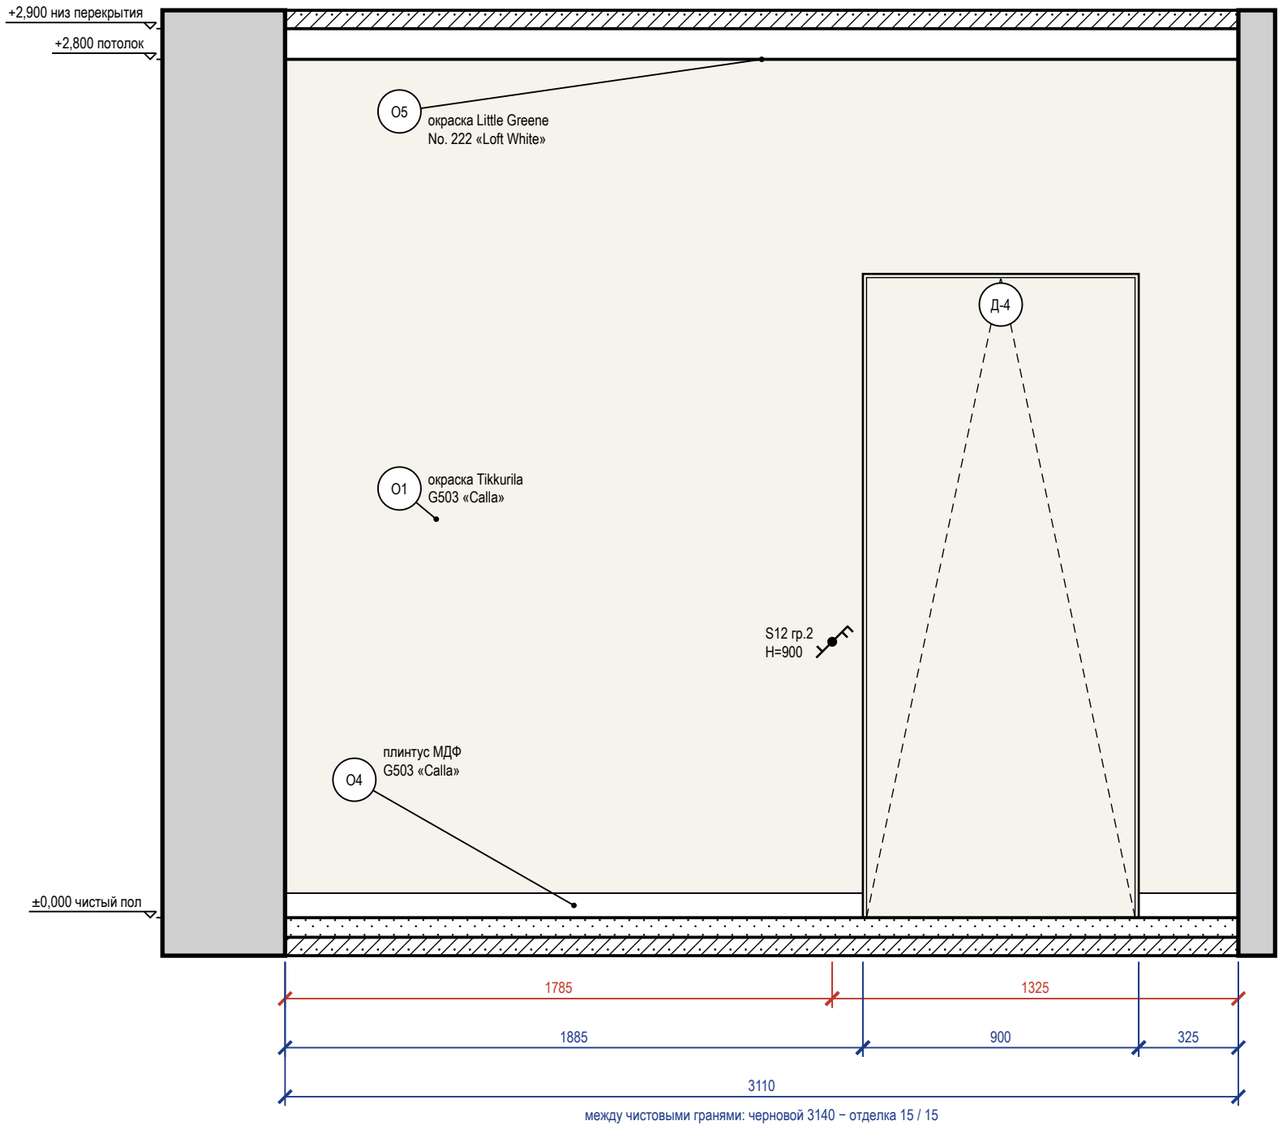


Схема развёрток (М 1:100)

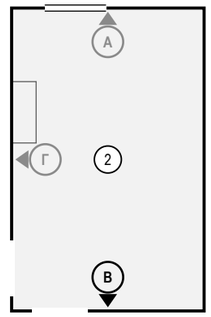

Ведомость отделки (на листе)

Марка	Поверхность	Материал, изделие	Цвет, код	Кол.
О1	стены	окраска, Tikkurila, матовая, подготовка Q3	Tikkurila G503 «Calla»	6,8 м²
О4	плинтус	плинтус МДФ, h 80 мм, аналог: плинтус МДФ под покраску 80×16	Tikkurila G503 «Calla»	2,2 м
О5	потолок	окраска, Little Greene Absolute Matt, глубокоматовая, подготовка Q3	Little Greene No. 222 «Loft White»	15,5 м²

Примечания

1. Размеры — в мм от чистовых поверхностей стен; условные обозначения и общие указания — лист 3.
2. Двери скрытого монтажа — полотно в плоскости стены, отделка стены по полотну, плинтус прерывается у короба (узел — на листе узлов).

					Проект: Дом 120 м² — М 1:20
	Лист	№ док.	Подпись	Дата	Развёртка стены В. Холл с лестницей (пом. 2)
Дизайнер	Кырлан А.С.			04.11.26	

Стадия	Лист	Листов
П	77	136

Развёртка стены Г


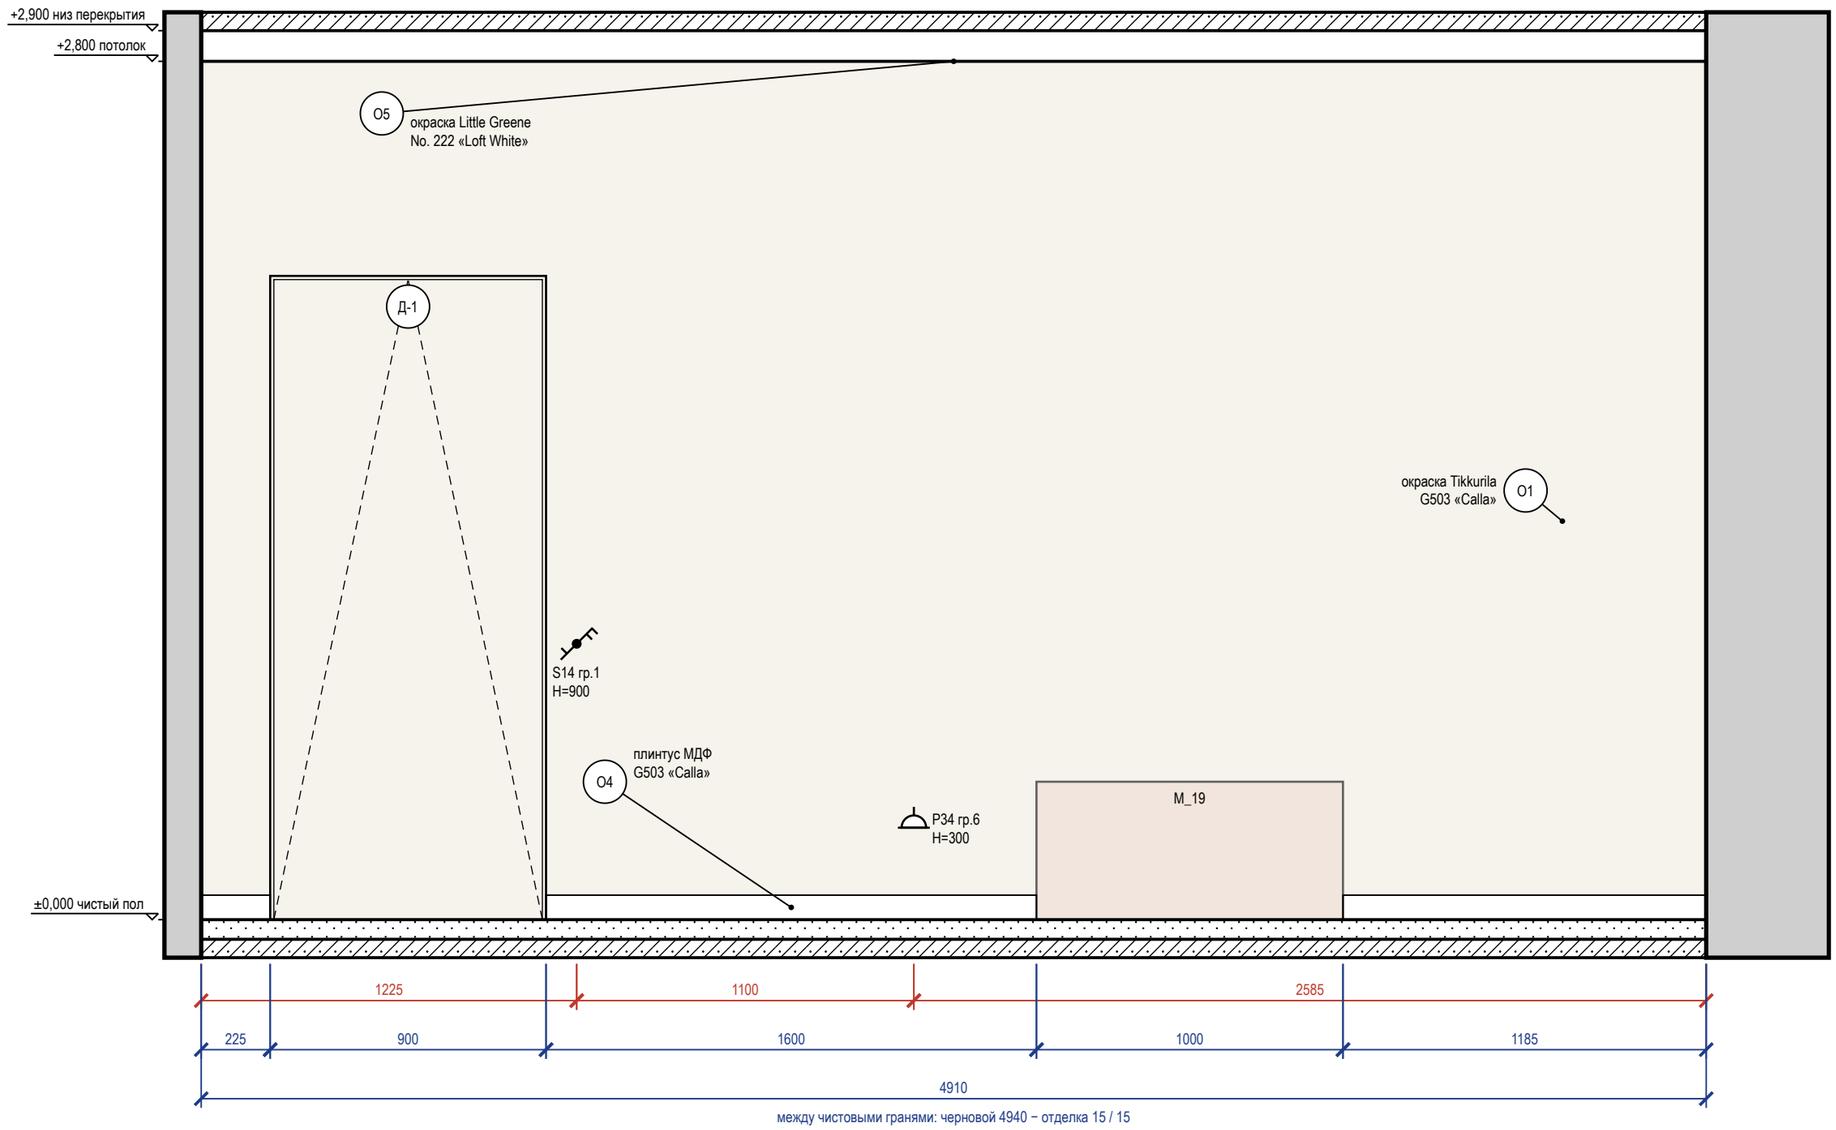


Схема развёрток (М 1:100)

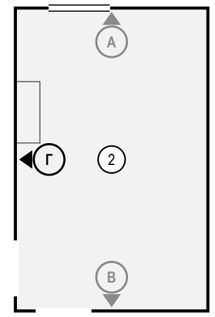

Ведомость отделки (на листе)

Марка	Поверхность	Материал, изделие	Цвет, код	Кол.
О1	стены	окраска, Tikkurila, матовая, подготовка Q3	Tikkurila G503 «Calla»	11,9 м²
О4	плинтус	плинтус МДФ, h 80 мм, аналог: плинтус МДФ под покраску 80×16	Tikkurila G503 «Calla»	3 м
О5	потолок	окраска, Little Greene Absolute Matt, глубокоматовая, подготовка Q3	Little Greene No. 222 «Loft White»	15,5 м²

Примечания

1. Размеры — в мм от чистовых поверхностей стен; условные обозначения и общие указания — лист 3.
2. Двери скрытого монтажа — полотно в плоскости стены, отделка стены по полотну, плинтус прерывается у короба (узел — на листе узлов).

					Проект: Дом 120 м²	М 1:20
	Лист	№ док.	Подпись	Дата		
Дизайнер	Кырлан А.С.			04.11.26	Развёртка стены Г. Холл с лестницей (пом. 2)	Стадия: П; Лист: 78; Листов: 136

Развёртка стены А


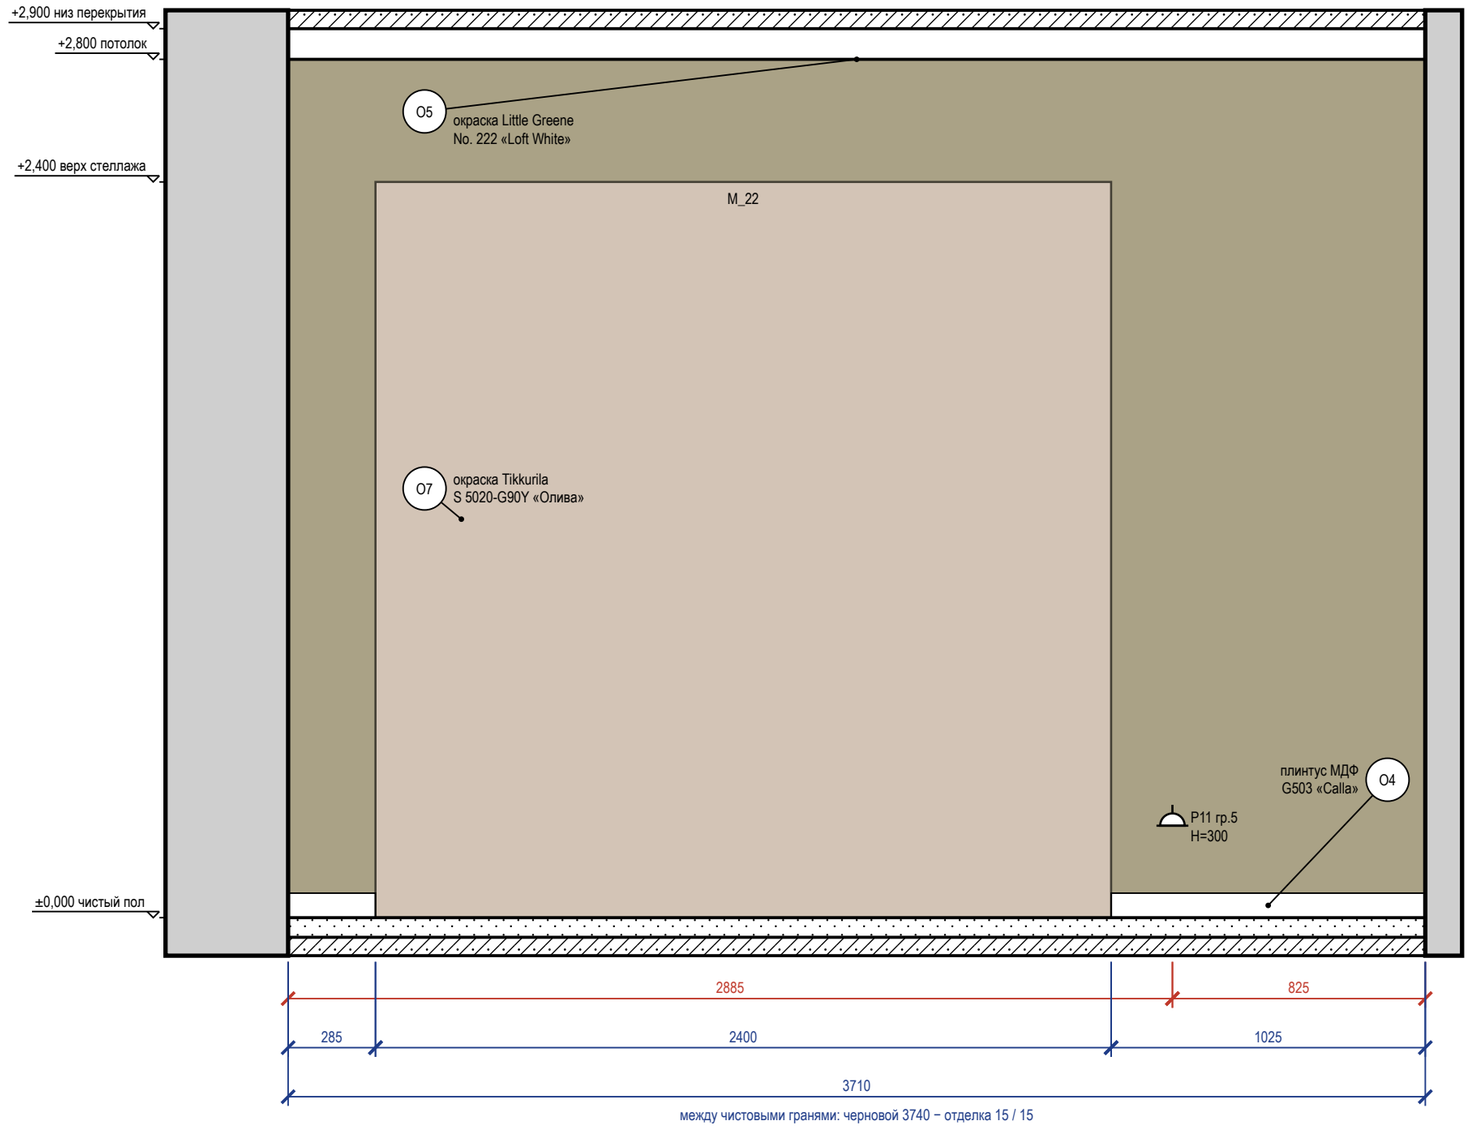


Схема развёрток (М 1:100)

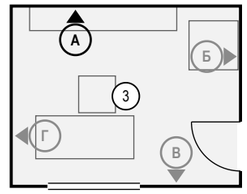

Ведомость отделки (на листе)


Марка	Поверхность	Материал, изделие	Цвет, код	Кол.
О4	плинтус	плинтус МДФ, h 80 мм, аналог: плинтус МДФ под покраску 80×16	Tikkurila G503 «Calla»	1,3 м
О5	потолок	окраска, Little Greene Absolute Matt, глубокоматовая, подготовка Q3	Little Greene No. 222 «Loft White»	11 м²
О7	акцентная стена	окраска, Tikkurila, матовая, подготовка Q3	NCS S 5020-G90Y «Олива»	10,4 м²

Примечания

1. Размеры — в мм от чистовых поверхностей стен; условные обозначения и общие указания — лист 3.
2. Потолок — у каждой стены свой, по плану потолков (ПТ3); ступени — зоной, кромка короба перед нишей — тонкой линией; в поле потолка: ПТ4 +2,650.


					Проект: Дом 120 м² — М 1:20
	Лист	№ док.	Подпись	Дата	Развёртка стены А. Кабинет (пом. 3)
Дизайнер	Кырлан А.С.			04.11.26	Стадия: П; Лист: 79; Листов: 136

Развёртка стены Б

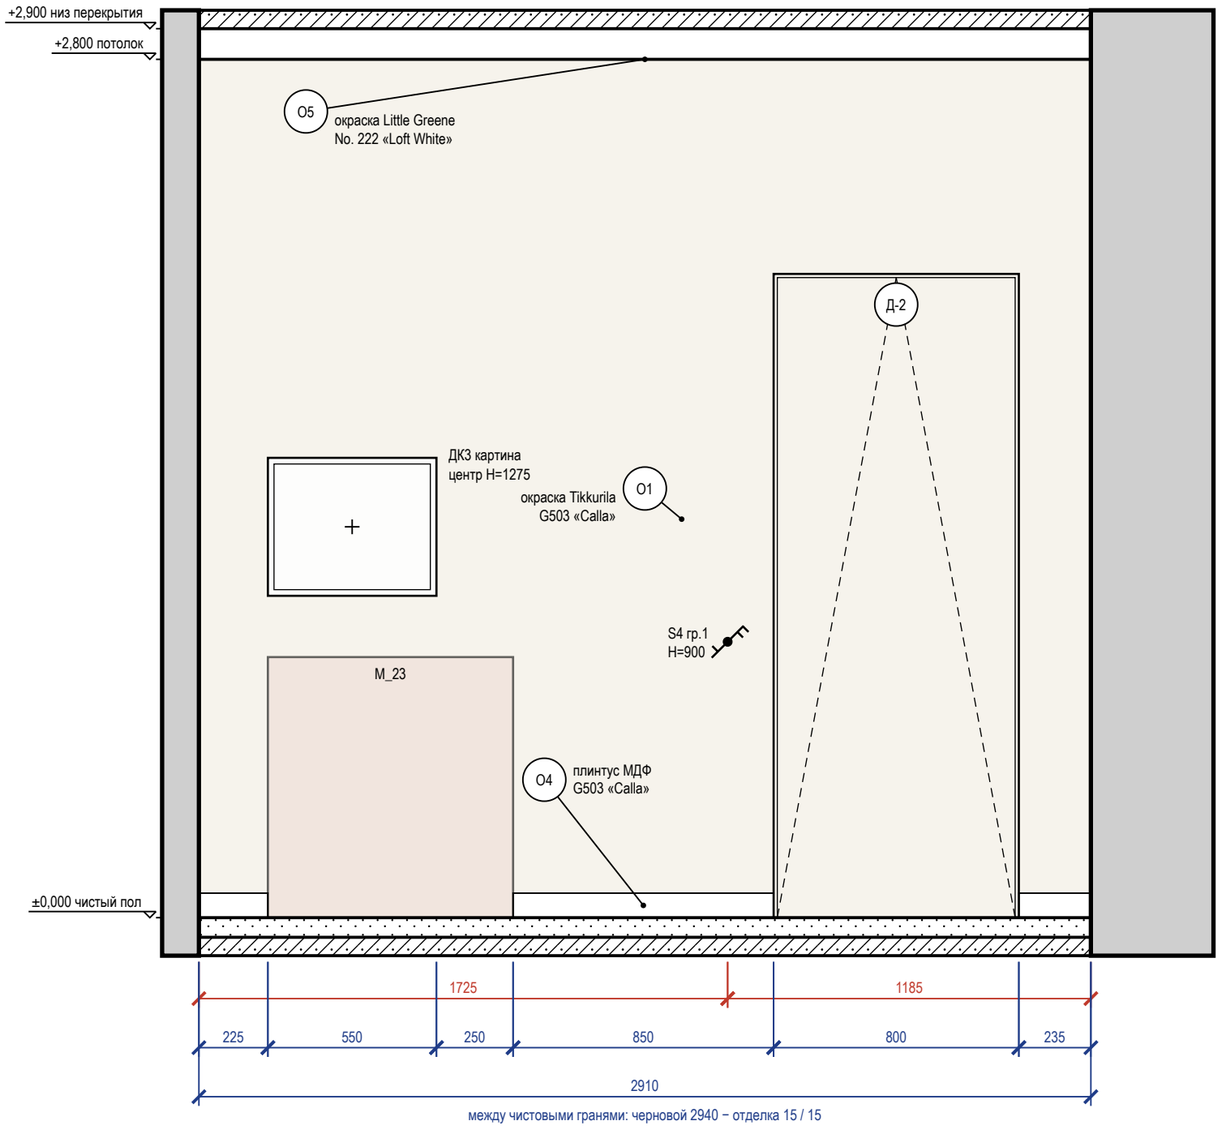

между чистовыми гранями: черновой 2940 − отделка 15 / 15

Схема развёрток (М 1:100)

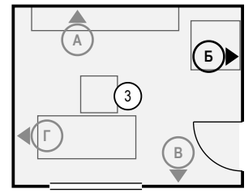

Ведомость отделки (на листе)


Марка	Поверхность	Материал, изделие	Цвет, код	Кол.
О1	стены	окраска, Tikkurila, матовая, подготовка Q3	Tikkurila G503 «Calla»	6,5 м²
О4	плинтус	плинтус МДФ, h 80 мм, аналог: плинтус МДФ под покраску 80×16	Tikkurila G503 «Calla»	1,3 м
О5	потолок	окраска, Little Greene Absolute Matt, глубокоматовая, подготовка Q3	Little Greene No. 222 «Loft White»	11 м²

Примечания

1. Размеры — в мм от чистовых поверхностей стен; условные обозначения и общие указания — лист 3.
2. Картины и зеркала крепить к основанию по паспорту изделия (закладные и анкеры — в перечне скрытых работ); крест — ось центра предмета.
3. Двери скрытого монтажа — полотно в плоскости стены, отделка стены по полотну, плинтус прерывается у короба (узел — на листе узлов).
4. Потолок — у каждой стены свой, по плану потолков (ПТ3); ступени — зоной, кромка короба перед нишей — тонкой линией; в поле потолка: ПТ4 +2,650.


					Проект: Дом 120 м²	М 1:20
	Лист	№ док.	Подпись	Дата		
Дизайнер	Кырлан А.С.			04.11.26	Развёртка стены Б. Кабинет (пом. 3)	
					Стадия: П	Лист: 80 / Листов: 136

Развёртка стены В

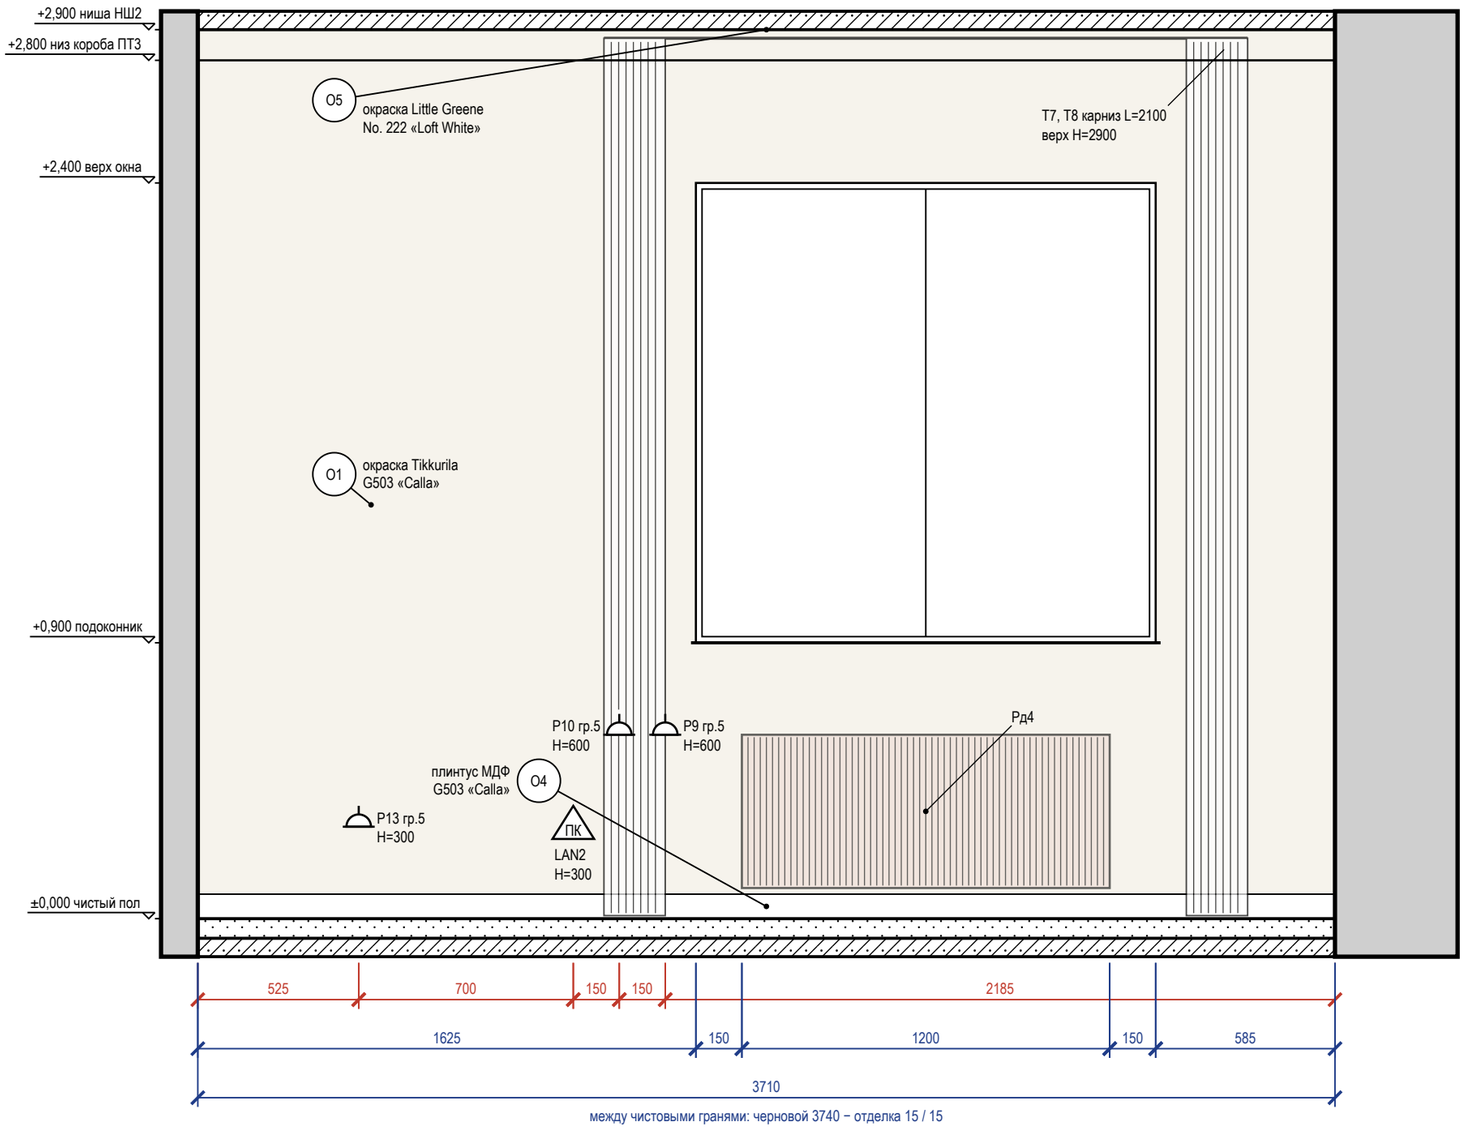

между чистовыми гранями: черновой 3740 − отделка 15 / 15

Схема развёрток (М 1:100)

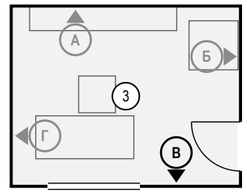

Ведомость отделки (на листе)

Марка	Поверхность	Материал, изделие	Цвет, код	Кол.
О1	стены	окраска, Tikkurila, матовая, подготовка Q3	Tikkurila G503 «Calla»	8,5 м²
О4	плинтус	плинтус МДФ, h 80 мм, аналог: плинтус МДФ под покраску 80×16	Tikkurila G503 «Calla»	3,7 м
О5	потолок	окраска, Little Greene Absolute Matt, глубокоматовая, подготовка Q3	Little Greene No. 222 «Loft White»	11 м²

Примечания

1. Размеры — в мм от чистовых поверхностей стен; условные обозначения и общие указания — лист 3.
2. Карнизы (шины) — по ведомости текстиля декоратора: длина L и верх Н на развёртке — те же числа, что в ведомости; крепление — до окраски потолка.
3. Потолок — у каждой стены свой, по плану потолков (НШ2, ПТ3); ступени — зоной, кромка короба перед нишей — тонкой линией; в поле потолка: ПТ4 +2,650.
4. Линии узора (швы плитки, складки штор, рёбра радиаторов) прерываются у знаков и выносок — просвет между линиями не менее 0,7 мм.

					Проект: Дом 120 м² — М 1:20
	Лист	№ док.	Подпись	Дата	Развёртка стены В. Кабинет (пом. 3)
Дизайнер	Кырлан А.С.			04.11.26	

Стадия	Лист	Листов
П	81	136

Развёртка стены Г


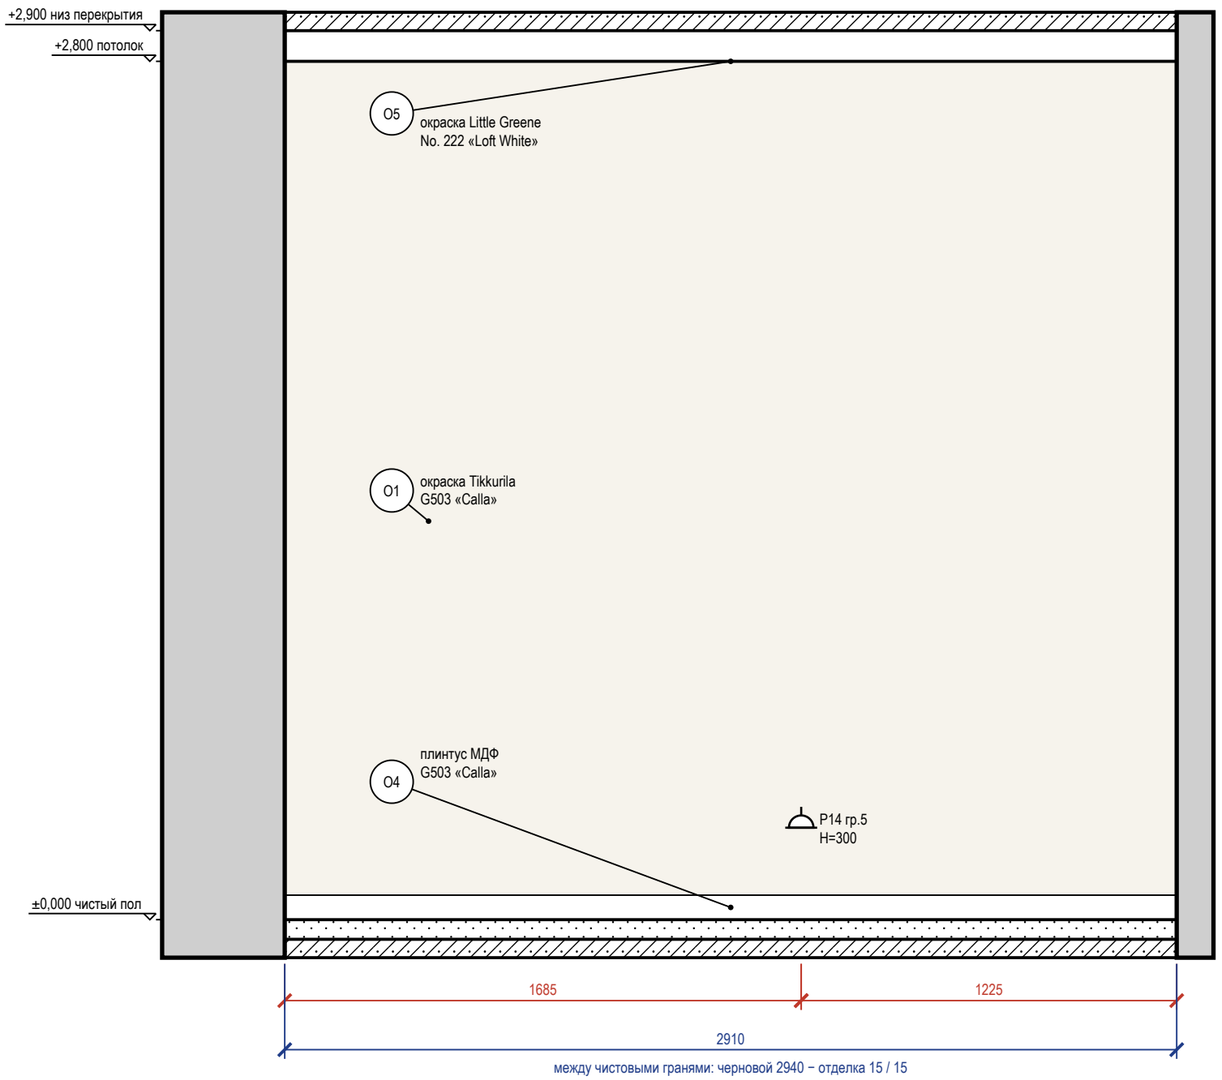


Схема развёрток (М 1:100)

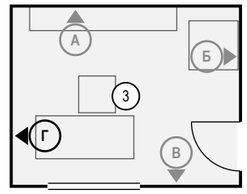

Ведомость отделки (на листе)


Марка	Поверхность	Материал, изделие	Цвет, код	Кол.
О1	стены	окраска, Tikkurila, матовая, подготовка Q3	Tikkurila G503 «Calla»	8,1 м²
О4	плинтус	плинтус МДФ, h 80 мм, аналог: плинтус МДФ под покраску 80×16	Tikkurila G503 «Calla»	2,9 м
О5	потолок	окраска, Little Greene Absolute Matt, глубокоматовая, подготовка Q3	Little Greene No. 222 «Loft White»	11 м²

Примечания

1. Размеры — в мм от чистовых поверхностей стен; условные обозначения и общие указания — лист 3.
2. Потолок — у каждой стены свой, по плану потолков (ПТ3); ступени — зоной, кромка короба перед нишей — тонкой линией; в поле потолка: ПТ4 +2,650.

					Проект: Дом 120 м²	М 1:20
	Лист	№ док.	Подпись	Дата		
Дизайнер	Кырлан А.С.			04.11.26	Развёртка стены Г. Кабинет (пом. 3)	Стадия: П; Лист: 82; Листов: 136

Развёртка стены А

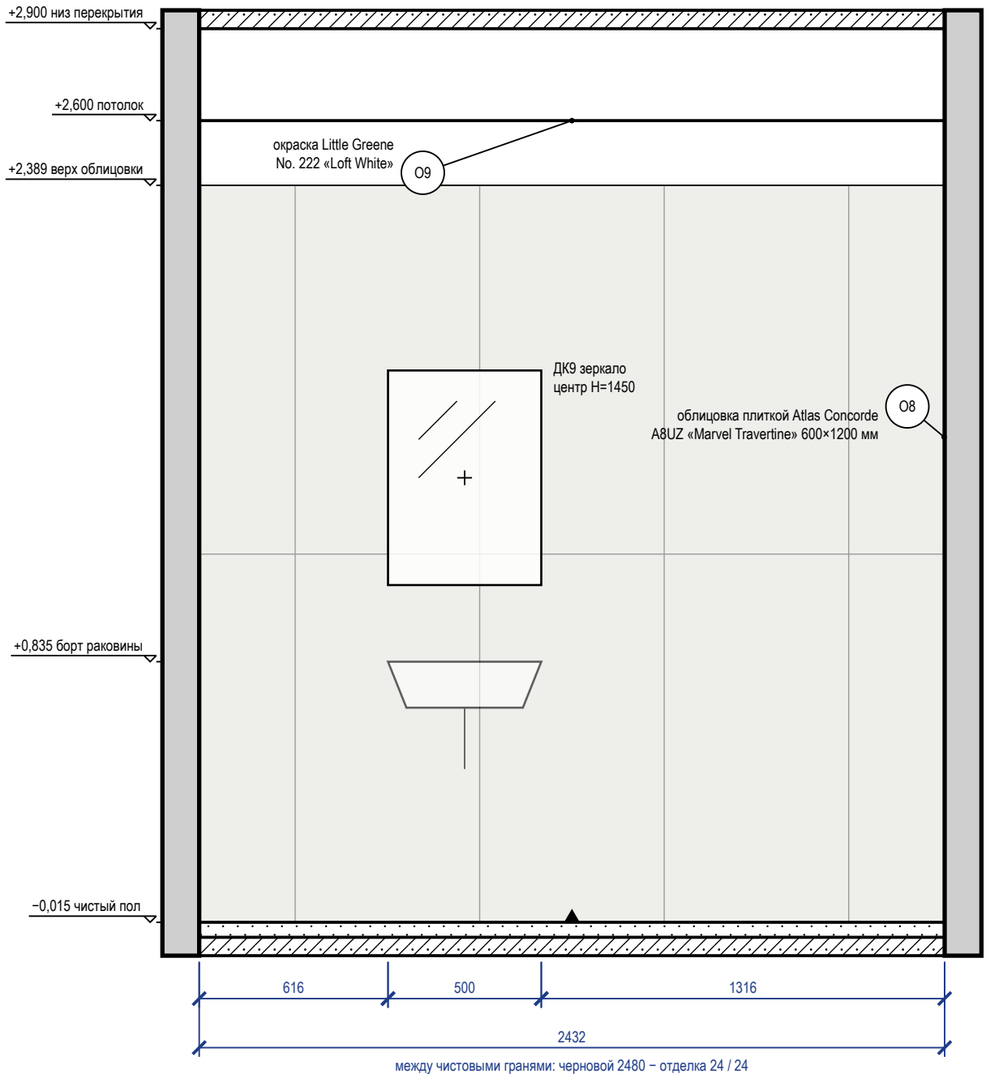

Развёртка стены Б


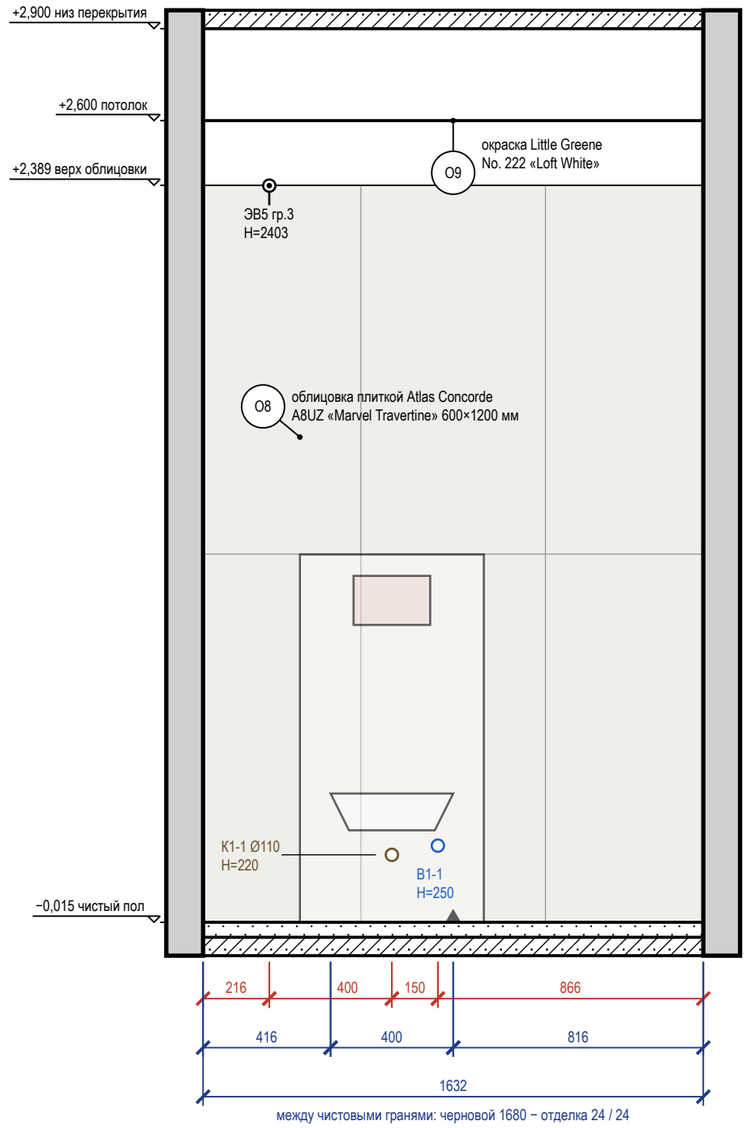


Схема развёрток (М 1:100)

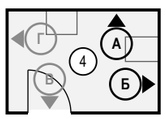

Ведомость отделки (на листе)

Марка	Поверхность	Материал, изделие	Цвет, код	Кол.
O8	стены	облицовка плиткой, Atlas Concorde Marvel Travertine, 600×1200×9 мм, A8UZ, затирка CG2WA	Atlas Concorde A8UZ «Marvel Travertine»	9,8 м²
O9	потолок	окраска, Little Greene Intelligent Bathroom, матовая, подготовка Q3	Little Greene No. 222 «Loft White»	4,2 м²

Примечания

1. Размеры — в мм от чистовых поверхностей стен; условные обозначения и общие указания — лист 3.
2. Стена А показана двумя видами: здесь — архитектурная развёртка (мебель, отделка, проёмы, высоты), электроточки и выводы ВК с привязками и таблицей — на листе 84 («Привязки»).
3. Схема мебели, приборов и декора не является технической документацией для производства мебели; габариты — по паспортам изделий.
4. Выводы ВК — коды и высоты по листу выводов сантехники.
5. Облицовка — по сетке швов 2 мм, раскладка от оси стены (треугольник у пола), целые ряды от пола; подрезки — по листу раскладки плитки.
6. Гидроизоляция в 2 слоя, заход на стены 200 мм — до облицовки, с актом скрытых работ и тестом проливом (узел — на листе узлов).
7. Картины и зеркала крепить к основанию по паспорту изделия (закладные и анкеры — в перечне скрытых работ); крест — ось центра предмета.

					Проект: Дом 120 м²	М 1:20
	Лист	№ док.	Подпись	Дата	Развёртки стен А, Б. Санузел гостевой (пом. 4)	
Дизайнер	Кырлан А.С.			04.11.26		

Стадия	Лист	Листов
П	83	136

выпуск 04.11.2026 № 406ed8a6ce · стр. 83 из 136

Развёртка стены А: электроточки и выводы

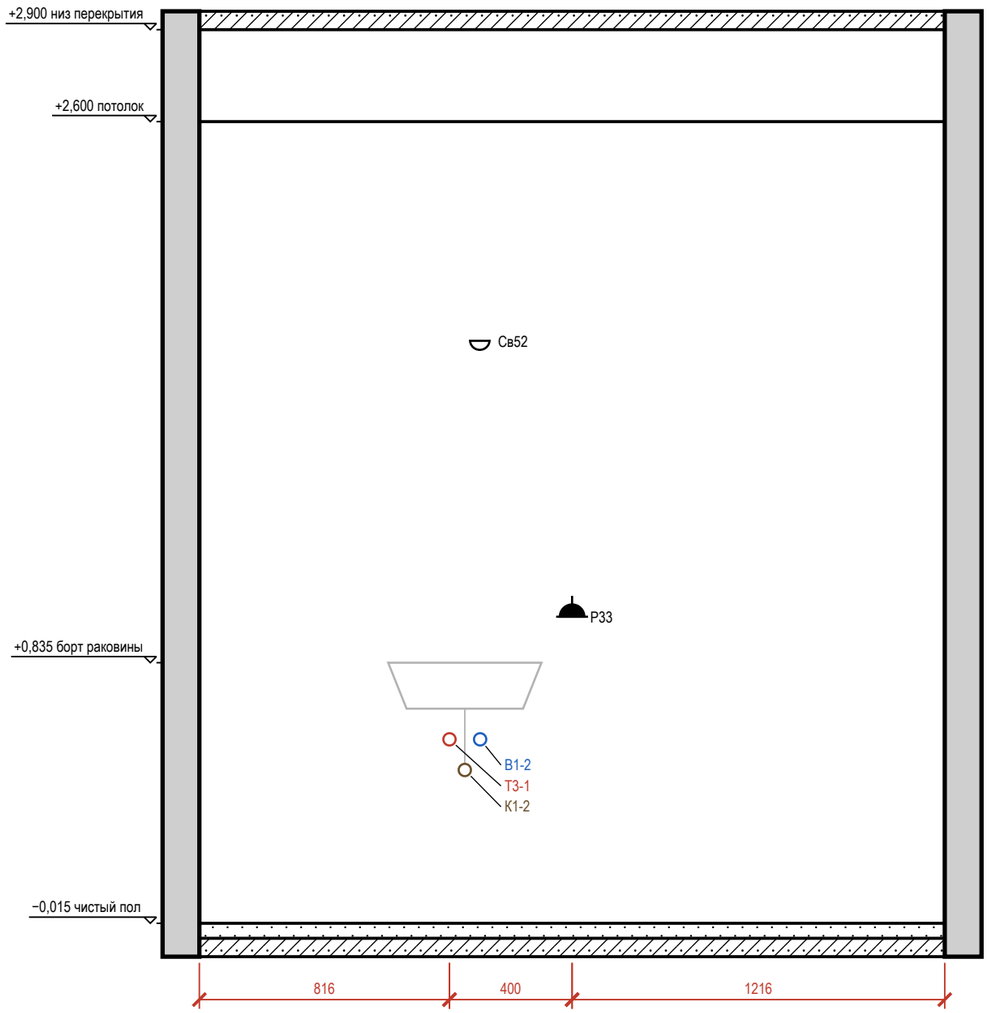



Таблица привязок электроточек и выводов

Марка	Назначение	От угла, мм	Н от пола, мм	Примечание
Т3-1	горячая вода — умывальник	816	600	межос. 100
К1-2	канализация — умывальник	866	500	Ø50
Св52	светильник настенный	915	1900	гр. 3
В1-2	холодная вода — умывальник	916	600	межос. 100
Р33	розетка: фен у умывальника	1216	1000	гр. 16, IP44

Условные обозначения

- розетка влагозащищённая IP44
- светильник настенный (бра), Н — высота оси
- вывод В1 (код — в ведомости привязок)
- вывод Т3 (код — в ведомости привязок)
- вывод К1 (код — в ведомости привязок)
- привязки точек и выводов от угла и от пола, мм
- марка развёртки: буква стены, стрелка — взгляд

Схема развёрток (М 1:50)

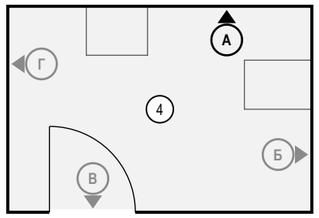


Примечания

1. Вид «Привязки» стены А — электроточки и выводы ВК; архитектурная развёртка (мебель, отделка, проёмы, высоты) — на листе 83. Мебель и приборы — подложкой для ориентира; их марки и обозначения мебели, проёмов и стен — там же.
2. Привязки — в мм: по горизонтали от левого чистового угла стены до оси изделия, Н — от чистого пола до оси; все точки — в таблице привязок. Красная цепочка — привязки по осям; точки ближе 120 мм одна к другой в цепочку не дробятся — их привязки только в таблице.
3. У знака — марка электроточки (Р — розетка, S — выключатель, Св — светильник, ЭВ — вывод кабеля); условные обозначения и общие указания — лист 3.
4. Коды выводов ВК: В1 — холодная вода, Т3 — горячая вода, К1 — канализация; номер после дефиса — номер вывода на листе выводов сантехники.


					Проект: Дом 120 м²	М 1:20
	Лист	№ док.	Подпись	Дата	Привязки электроточек и выводов ВК, стена А. Санузел гостевой (пом. 4)	Стадия / Лист / Листов
Дизайнер	Кырлан А.С.			04.11.26		П / 84 / 136

Развёртка стены В

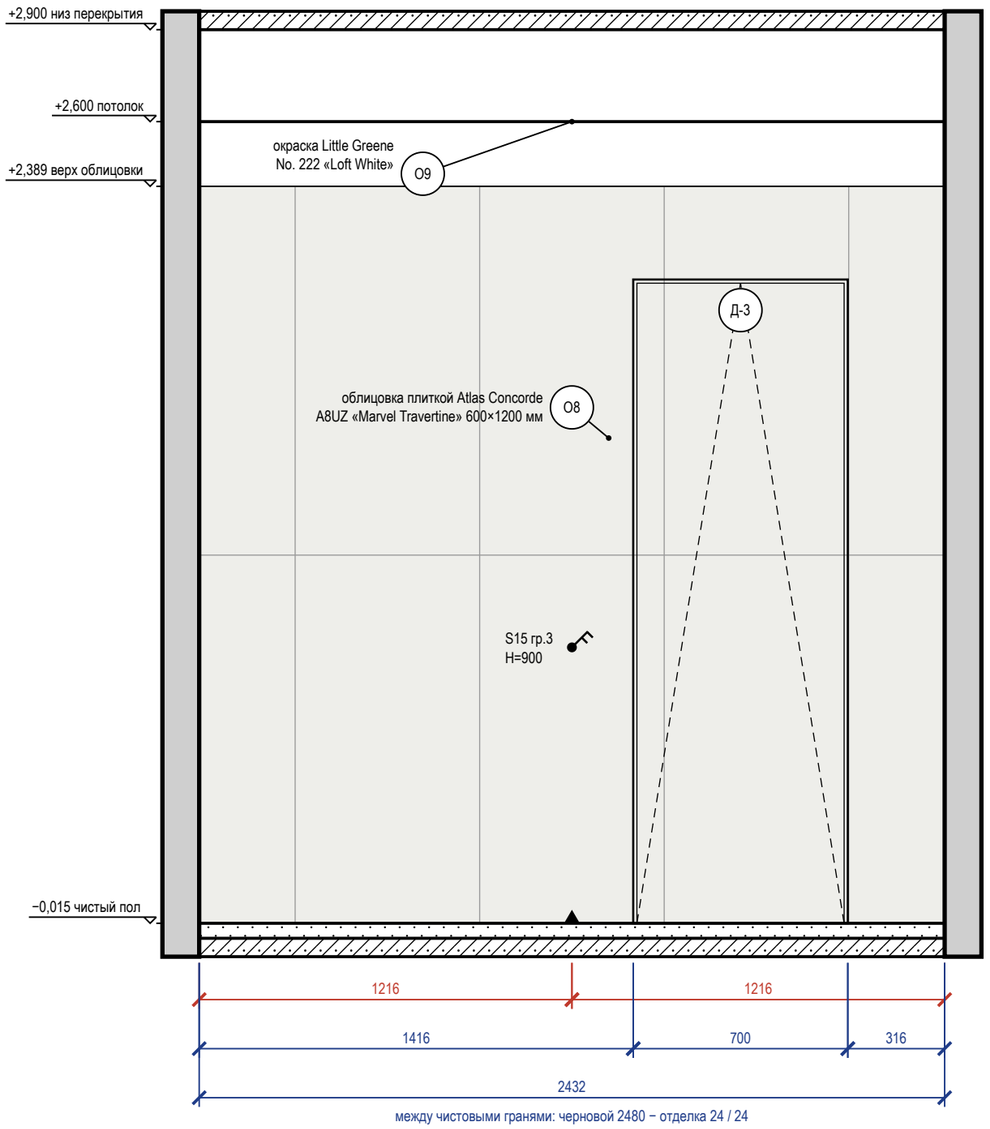


между чистовыми гранями: черновой 2480 − отделка 24 / 24

Развёртка стены Г

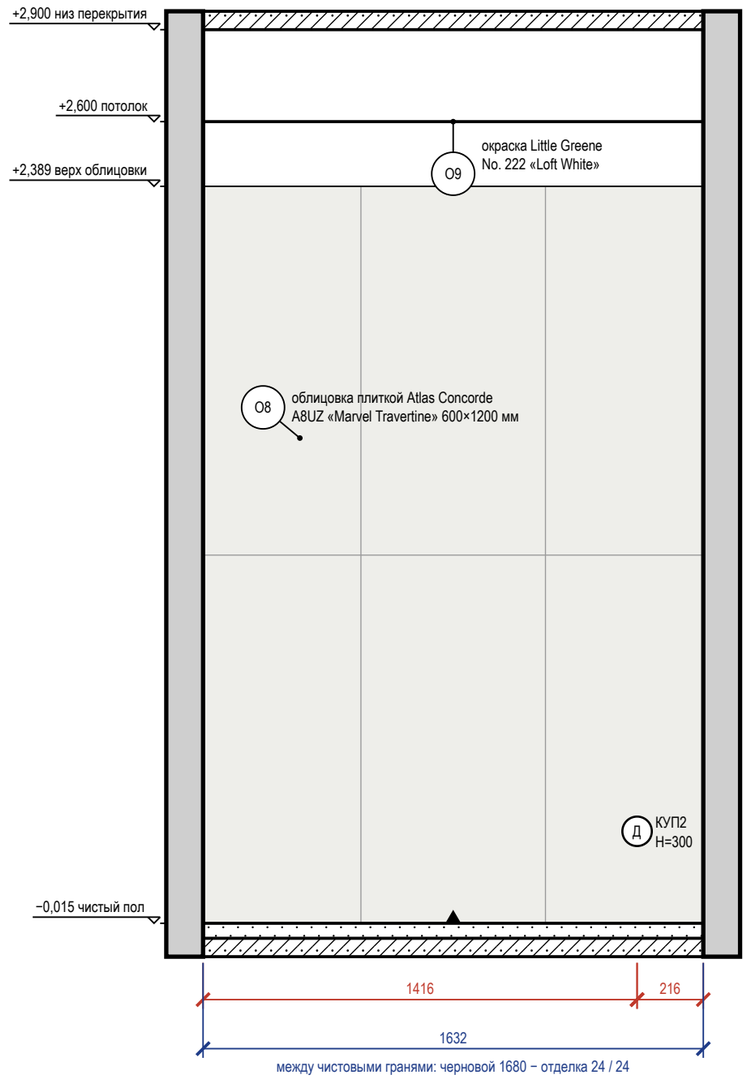

между чистовыми гранями: черновой 1680 − отделка 24 / 24

Схема развёрток (М 1:100)

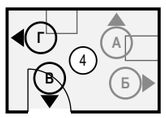

Ведомость отделки (на листе)

Марка	Поверхность	Материал, изделие	Цвет, код	Кол.
О8	стены	облицовка плиткой, Atlas Concorde Marvel Travertine, 600×1200×9 мм, A8UZ, затирка CG2WA	Atlas Concorde A8UZ «Marvel Travertine»	8,3 м²
О9	потолок	окраска, Little Greene Intelligent Bathroom, матовая, подготовка Q3	Little Greene No. 222 «Loft White»	4,2 м²

Примечания

1. Размеры — в мм от чистовых поверхностей стен; условные обозначения и общие указания — лист 3.
2. Облицовка — по сетке швов 2 мм, раскладка от оси стены (треугольник у пола), целые ряды от пола; подрезки — по листу раскладки плитки.
3. Гидроизоляция в 2 слоя, заход на стены 200 мм — до облицовки, с актом скрытых работ и тестом проливом (узел — на листе узлов).
4. Двери скрытого монтажа — полотно в плоскости стены, отделка стены по полотну, плинтус прерывается у короба (узел — на листе узлов).

					Проект: Дом 120 м²	М 1:20
	Лист	№ док.	Подпись	Дата	Развёртки стен В, Г. Санузел гостевой (пом. 4)	Стадия / Лист / Листов
Дизайнер	Кырлан А.С.			04.11.26		П / 85 / 136

Развёртка стены А1


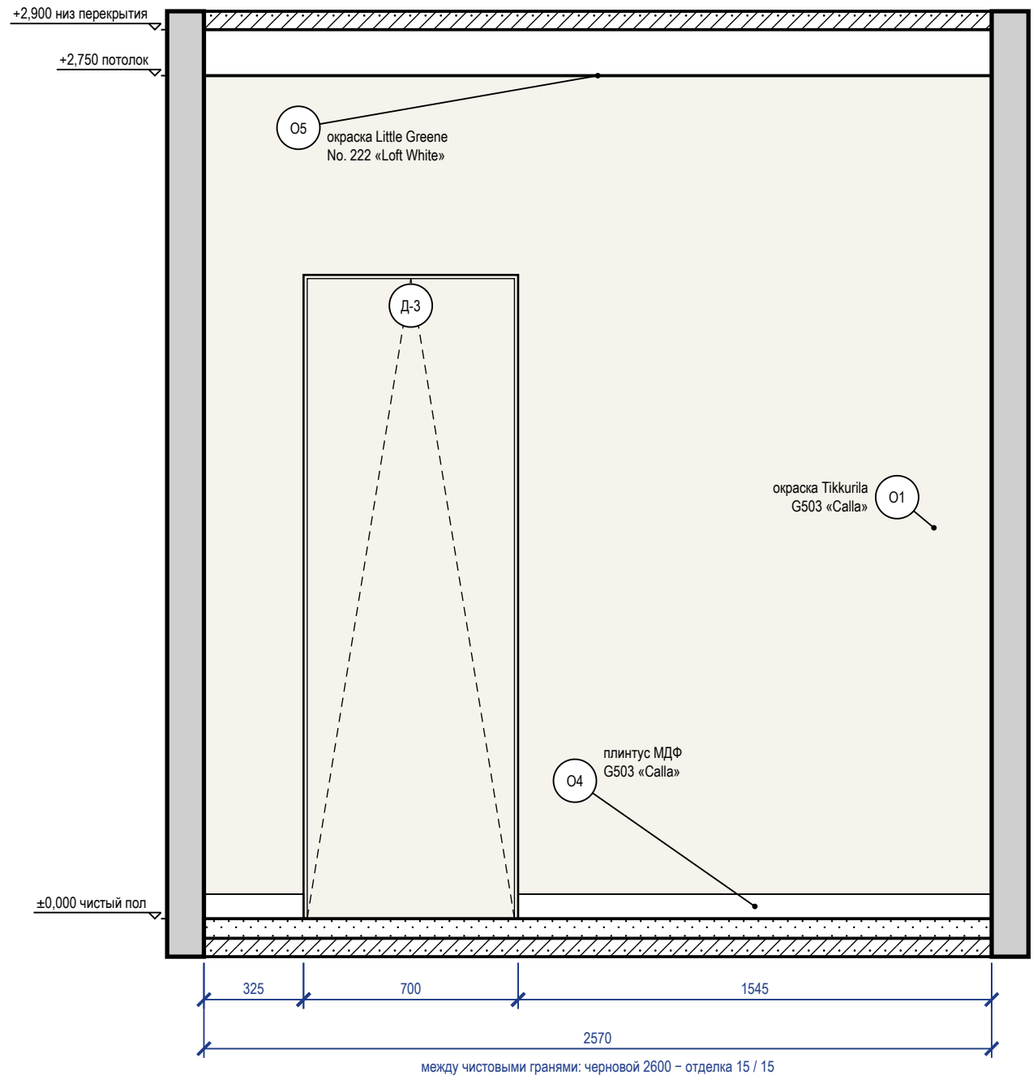


Схема развёрток (М 1:100)

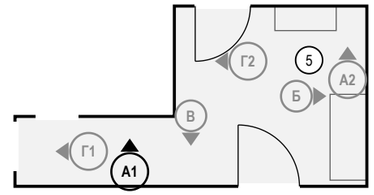

Ведомость отделки (на листе)

Марка	Поверхность	Материал, изделие	Цвет, код	Кол.
О1	стены	окраска, Tikkurila, матовая, подготовка Q3	Tikkurila G503 «Calla»	5,6 м²
О4	плинтус	плинтус МДФ, h 80 мм, аналог: плинтус МДФ под покраску 80×16	Tikkurila G503 «Calla»	1,9 м
О5	потолок	окраска, Little Greene Absolute Matt, глубокоматовая, подготовка Q3	Little Greene No. 222 «Loft White»	12,2 м²

Примечания

1. Размеры — в мм от чистовых поверхностей стен; условные обозначения и общие указания — лист 3.
2. Двери скрытого монтажа — полотно в плоскости стены, отделка стены по полотну, плинтус прерывается у короба (узел — на листе узлов).

	Лист	№ док.	Подпись	Дата
Дизайнер	Кырлан А.С.			04.11.26

Проект: Дом 120 м² — **М 1:20**

Развёртка стены А1. Прихожая (пом. 5)

Стадия	Лист	Листов
П	86	136

Развёртка стены А2


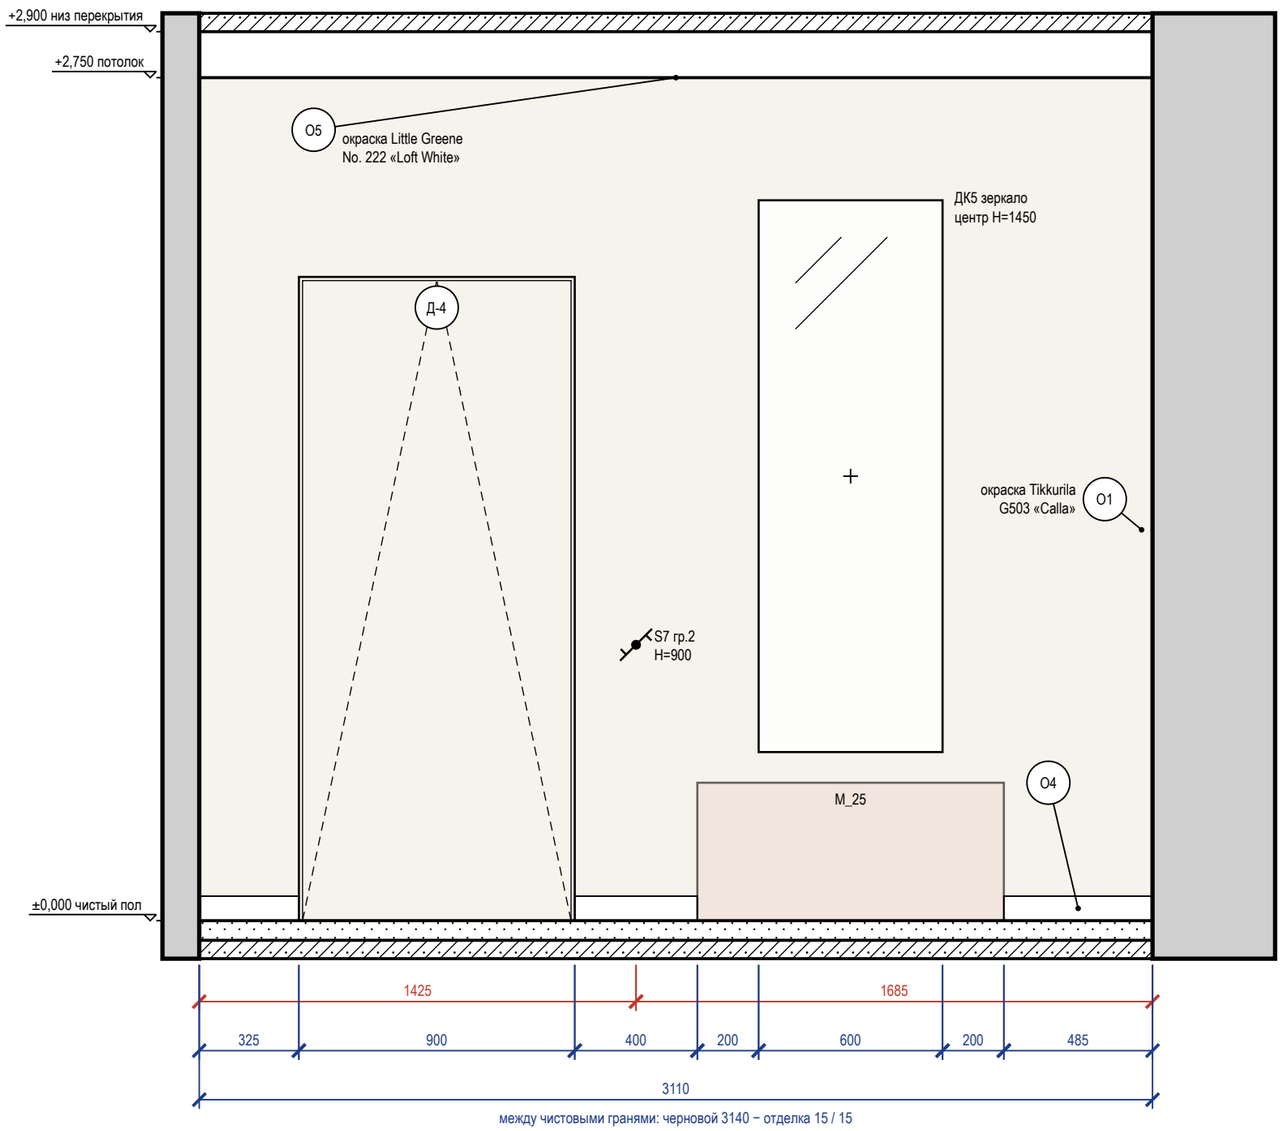


Схема развёрток (М 1:100)

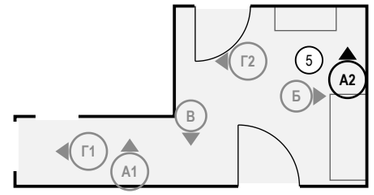

Ведомость отделки (на листе)

Марка	Поверхность	Материал, изделие	Цвет, код	Кол.
О1	стены	окраска, Tikkurila, матовая, подготовка Q3	Tikkurila G503 «Calla»	6,7 м²
О4	плинтус	плинтус МДФ, h 80 мм, аналог: плинтус МДФ под покраску 80×16	Tikkurila G503 «Calla»	1,2 м
О5	потолок	окраска, Little Greene Absolute Matt, глубокоматовая, подготовка Q3	Little Greene No. 222 «Loft White»	12,2 м²

Примечания

1. Размеры — в мм от чистовых поверхностей стен; условные обозначения и общие указания — лист 3.
2. Картины и зеркала крепить к основанию по паспорту изделия (закладные и анкеры — в перечне скрытых работ); крест — ось центра предмета.
3. Двери скрытого монтажа — полотно в плоскости стены, отделка стены по полотну, плинтус прерывается у короба (узел — на листе узлов).

					Проект: Дом 120 м² — М 1:20
	Лист	№ док.	Подпись	Дата	Развёртка стены А2. Прихожая (пом. 5)
Дизайнер	Кырлан А.С.			04.11.26	Стадия: П; Лист: 87; Листов: 136

Развёртка стены Б


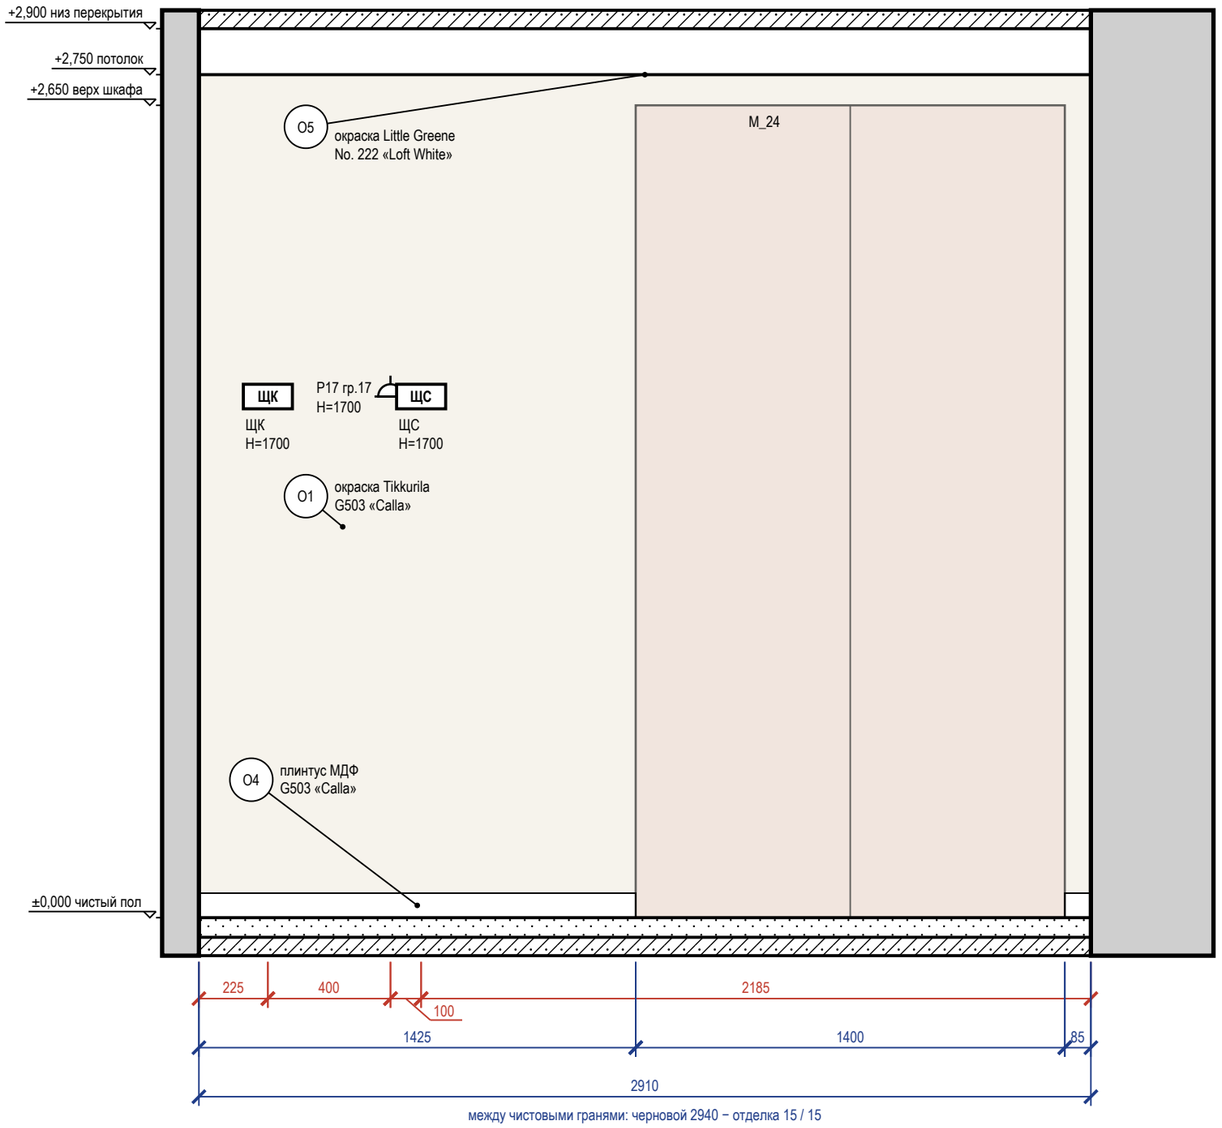


Схема развёрток (М 1:100)

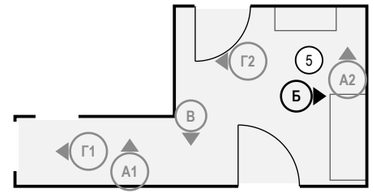

Ведомость отделки (на листе)


Марка	Поверхность	Материал, изделие	Цвет, код	Кол.
О1	стены	окраска, Tikkurila, матовая, подготовка Q3	Tikkurila G503 «Calla»	8 м²
О4	плинтус	плинтус МДФ, h 80 мм, аналог: плинтус МДФ под покраску 80×16	Tikkurila G503 «Calla»	1,5 м
О5	потолок	окраска, Little Greene Absolute Matt, глубокоматовая, подготовка Q3	Little Greene No. 222 «Loft White»	12,2 м²

Примечания

1. Размеры — в мм от чистовых поверхностей стен; условные обозначения и общие указания — лист 3.


					Проект: Дом 120 м²	М 1:20
	Лист	№ док.	Подпись	Дата		
Дизайнер	Кырлан А.С.			04.11.26	Развёртка стены Б. Прихожая (пом. 5)	Стадия: П; Лист: 88; Листов: 136

Развёртка стены В

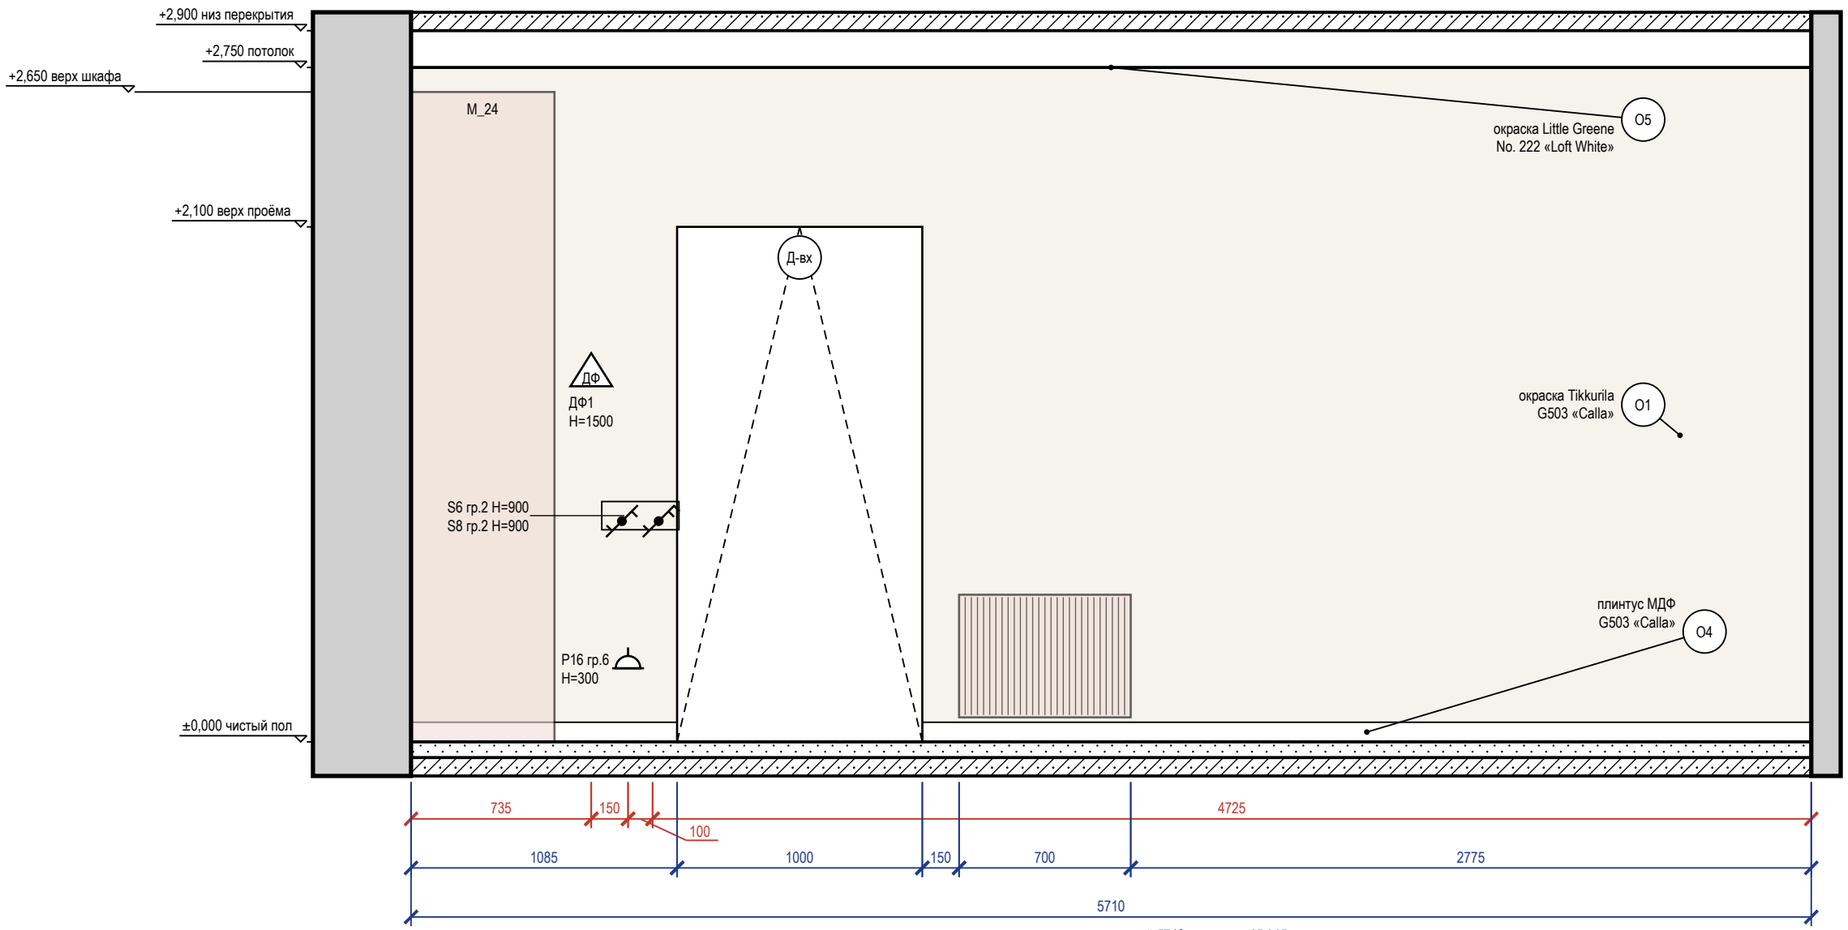

между чистовыми гранями: черновой 5740 − отделка 15 / 15

Схема развёрток (М 1:100)

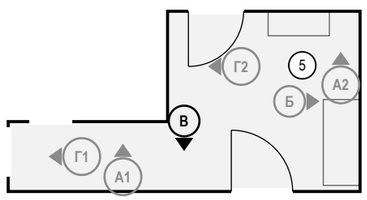

Ведомость отделки (на листе)


Марка	Поверхность	Материал, изделие	Цвет, код	Кол.
O1	стены	окраска, Tikkurila, матовая, подготовка Q3	Tikkurila G503 «Calla»	13,6 м²
O4	плинтус	плинтус МДФ, h 80 мм, аналог: плинтус МДФ под покраску 80×16	Tikkurila G503 «Calla»	4,7 м
O5	потолок	окраска, Little Greene Absolute Matt, глубокоматовая, подготовка Q3	Little Greene No. 222 «Loft White»	12,2 м²

Примечания

1. Размеры — в мм от чистовых поверхностей стен; условные обозначения и общие указания — лист 3.


					Проект: Дом 120 м²	М 1:25
	Лист	№ док.	Подпись	Дата		
Дизайнер	Кырлан А.С.			04.11.26	Развёртка стены В. Прихожая (пом. 5)	Стадия: П; Лист: 89; Листов: 136

Развёртка стены Г1

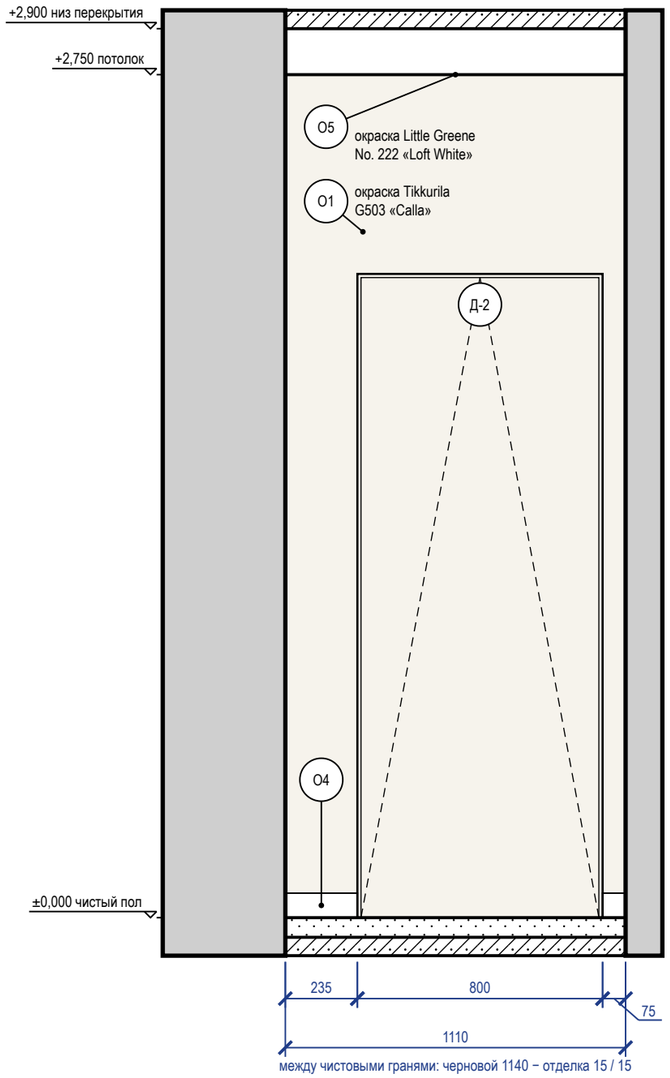


между чистовыми гранями: черновой 1140 − отделка 15 / 15

Развёртка стены Г2

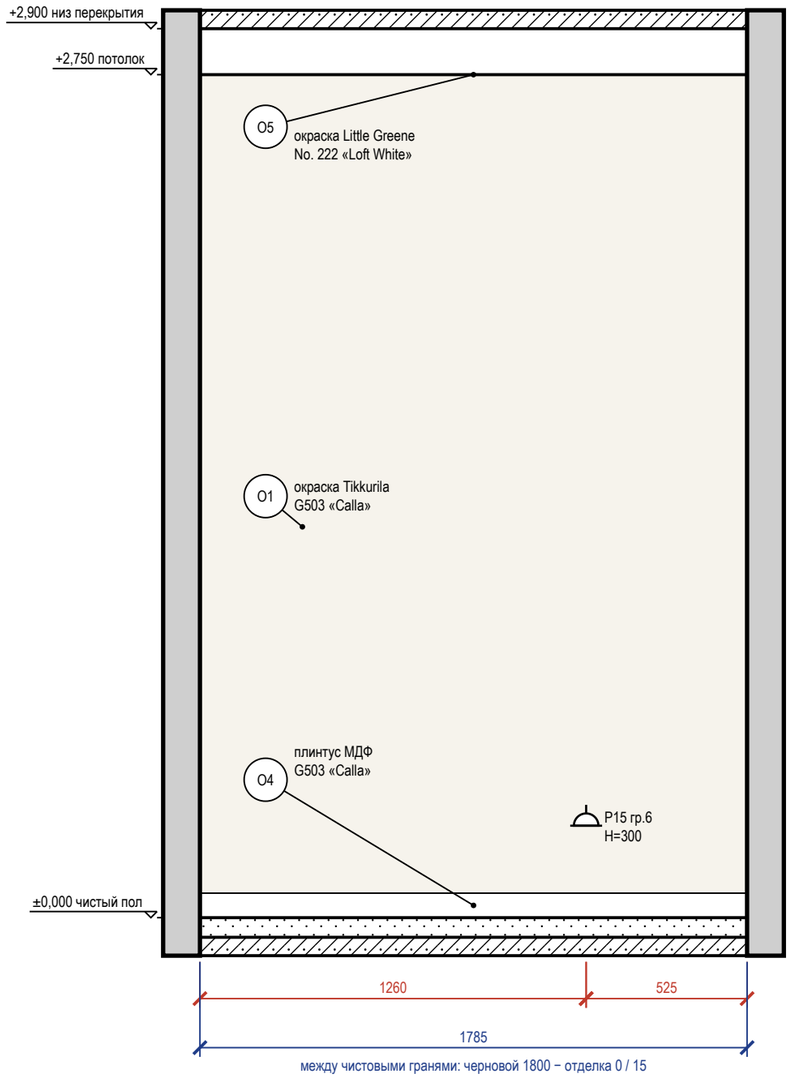

между чистовыми гранями: черновой 1800 − отделка 0 / 15

Схема развёрток (М 1:100)

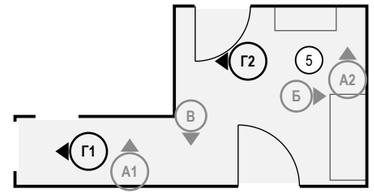

Ведомость отделки (на листе)

Марка	Поверхность	Материал, изделие	Цвет, код	Кол.
О1	стены	окраска, Tikkurila, матовая, подготовка Q3	Tikkurila G503 «Calla»	6,3 м²
О4	плинтус	плинтус МДФ, h 80 мм, аналог: плинтус МДФ под покраску 80×16	Tikkurila G503 «Calla»	2,1 м
О5	потолок	окраска, Little Greene Absolute Matt, глубокоматовая, подготовка Q3	Little Greene No. 222 «Loft White»	12,2 м²

Примечания

1. Размеры — в мм от чистовых поверхностей стен; условные обозначения и общие указания — лист 3.
2. Двери скрытого монтажа — полотно в плоскости стены, отделка стены по полотну, плинтус прерывается у короба (узел — на листе узлов).

					Проект: Дом 120 м²	М 1:20
	Лист	№ док.	Подпись	Дата		
Дизайнер	Кырлан А.С.			04.11.26	Развёртки стен Г1, Г2. Прихожая (пом. 5)	Стадия: П; Лист: 90; Листов: 136

Развёртка стены А


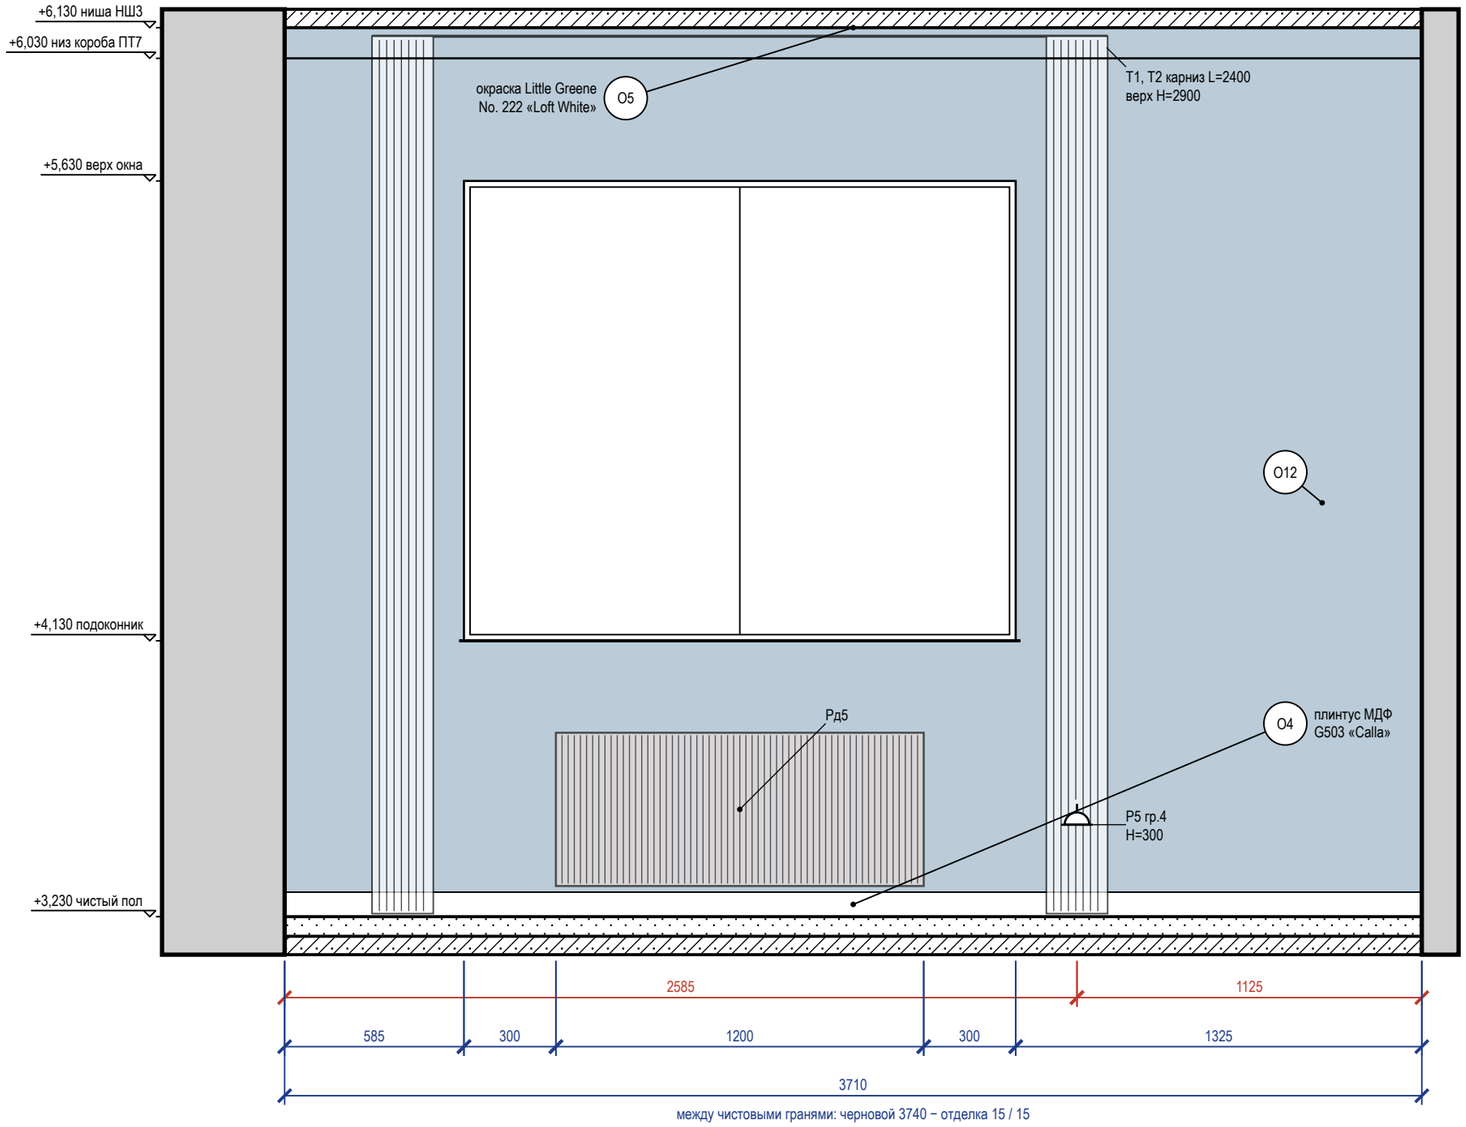


Схема развёрток (М 1:100)

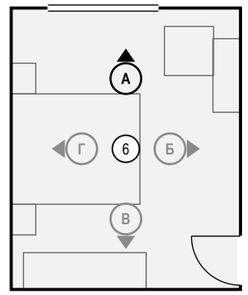

Ведомость отделки (на листе)

Марка	Поверхность	Материал, изделие	Цвет, код	Кол.
О4	плинтус	плинтус МДФ, h 80 мм, аналог: плинтус МДФ под покраску 80×16	Tikkurila G503 «Calla»	3,7 м
О5	потолок	окраска, Little Greene Absolute Matt, глубокоматовая, подготовка Q3	Little Greene No. 222 «Loft White»	17,2 м²
О12	акцентная стена	окраска, Farrow & Ball Modern Emulsion, матовая, подготовка Q3	Farrow & Ball No. 89 «Lulworth Blue — светлая морская лазурь»	8,1 м²

Примечания

1. Размеры — в мм от чистовых поверхностей стен; условные обозначения и общие указания — лист 3.
2. Карнизы (шины) — по ведомости текстиля декоратора: длина L и верх H на развёртке — те же числа, что в ведомости; крепление — до окраски потолка.
3. Потолок — у каждой стены свой, по плану потолков (НШ3, ПТ7); ступени — зоной, кромка короба перед нишей — тонкой линией; в поле потолка: ПТ6 +5,880.
4. Линии узора (швы плитки, складки штор, рёбра радиаторов) прерываются у знаков и выносок — просвет между линиями не менее 0,7 мм.

	Лист	№ док.	Подпись	Дата
Дизайнер	Кырлан А.С.			04.11.26

Проект: Дом 120 м² — М 1:20

Развёртка стены А. Спальня родителей (пом. 6)

Стадия	Лист	Листов
П	91	136

выпуск 04.11.2026 № 406ed8a6ce · стр. 91 из 136

Развёртка стены Б


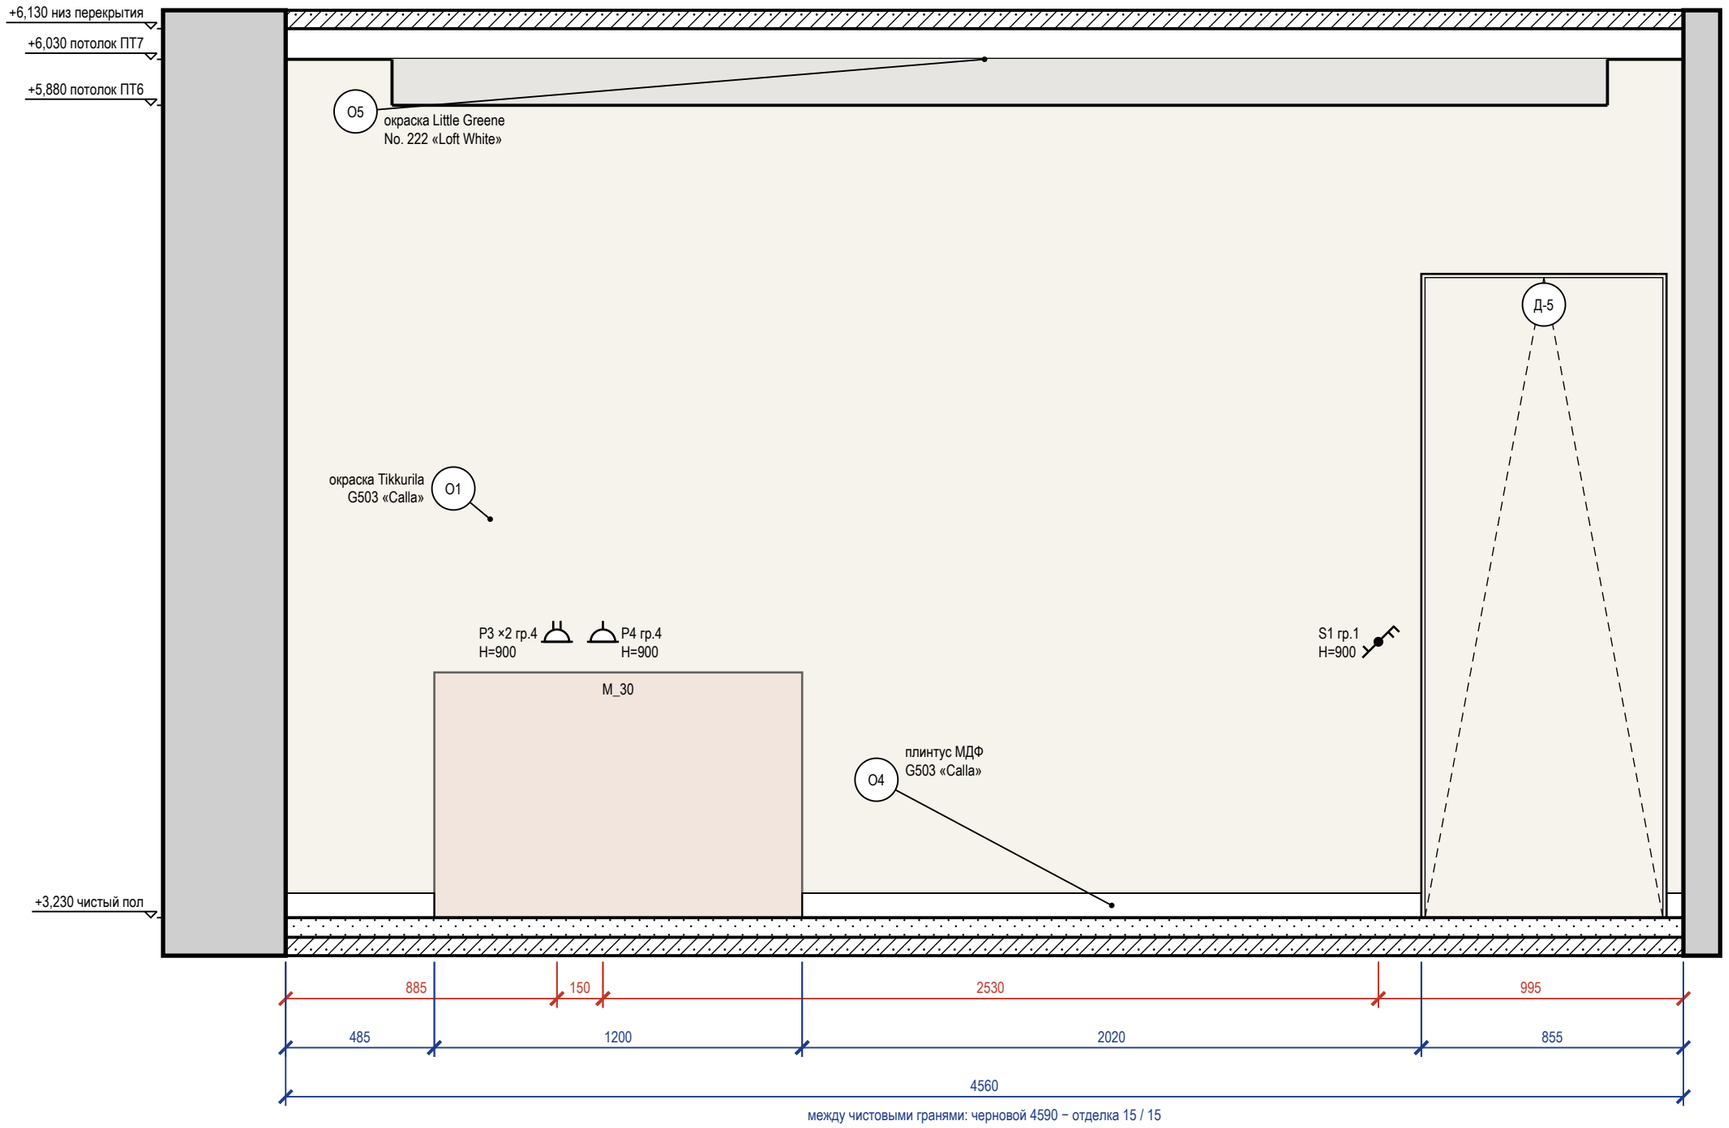


Схема разверток (М 1:100)

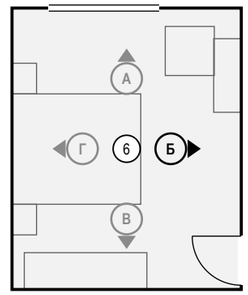

Ведомость отделки (на листе)

Марка	Поверхность	Материал, изделие	Цвет, код	Кол.
О1	стены	окраска, Tikkurila, матовая, подготовка Q3	Tikkurila G503 «Calla»	11,1 м²
О4	плинтус	плинтус МДФ, h 80 мм, аналог: плинтус МДФ под покраску 80×16	Tikkurila G503 «Calla»	2,6 м
О5	потолок	окраска, Little Greene Absolute Matt, глубокоматовая, подготовка Q3	Little Greene No. 222 «Loft White»	17,2 м²

Примечания

1. Размеры — в мм от чистовых поверхностей стен; условные обозначения и общие указания — лист 3.
2. Двери скрытого монтажа — полотно в плоскости стены, отделка стены по полотну, плинтус прерывается у короба (узел — на листе узлов).
3. Потолок — у каждой стены свой, по плану потолков (ПТ7, ПТ6); ступени — зоной, кромка короба перед нишей — тонкой линией.

					Проект: Дом 120 м² — М 1:20
	Лист	№ док.	Подпись	Дата	
Дизайнер	Кырлан А.С.			04.11.26	Развёртка стены Б. Спальня родителей (пом. 6)

Стадия	Лист	Листов
П	92	136

Развёртка стены В


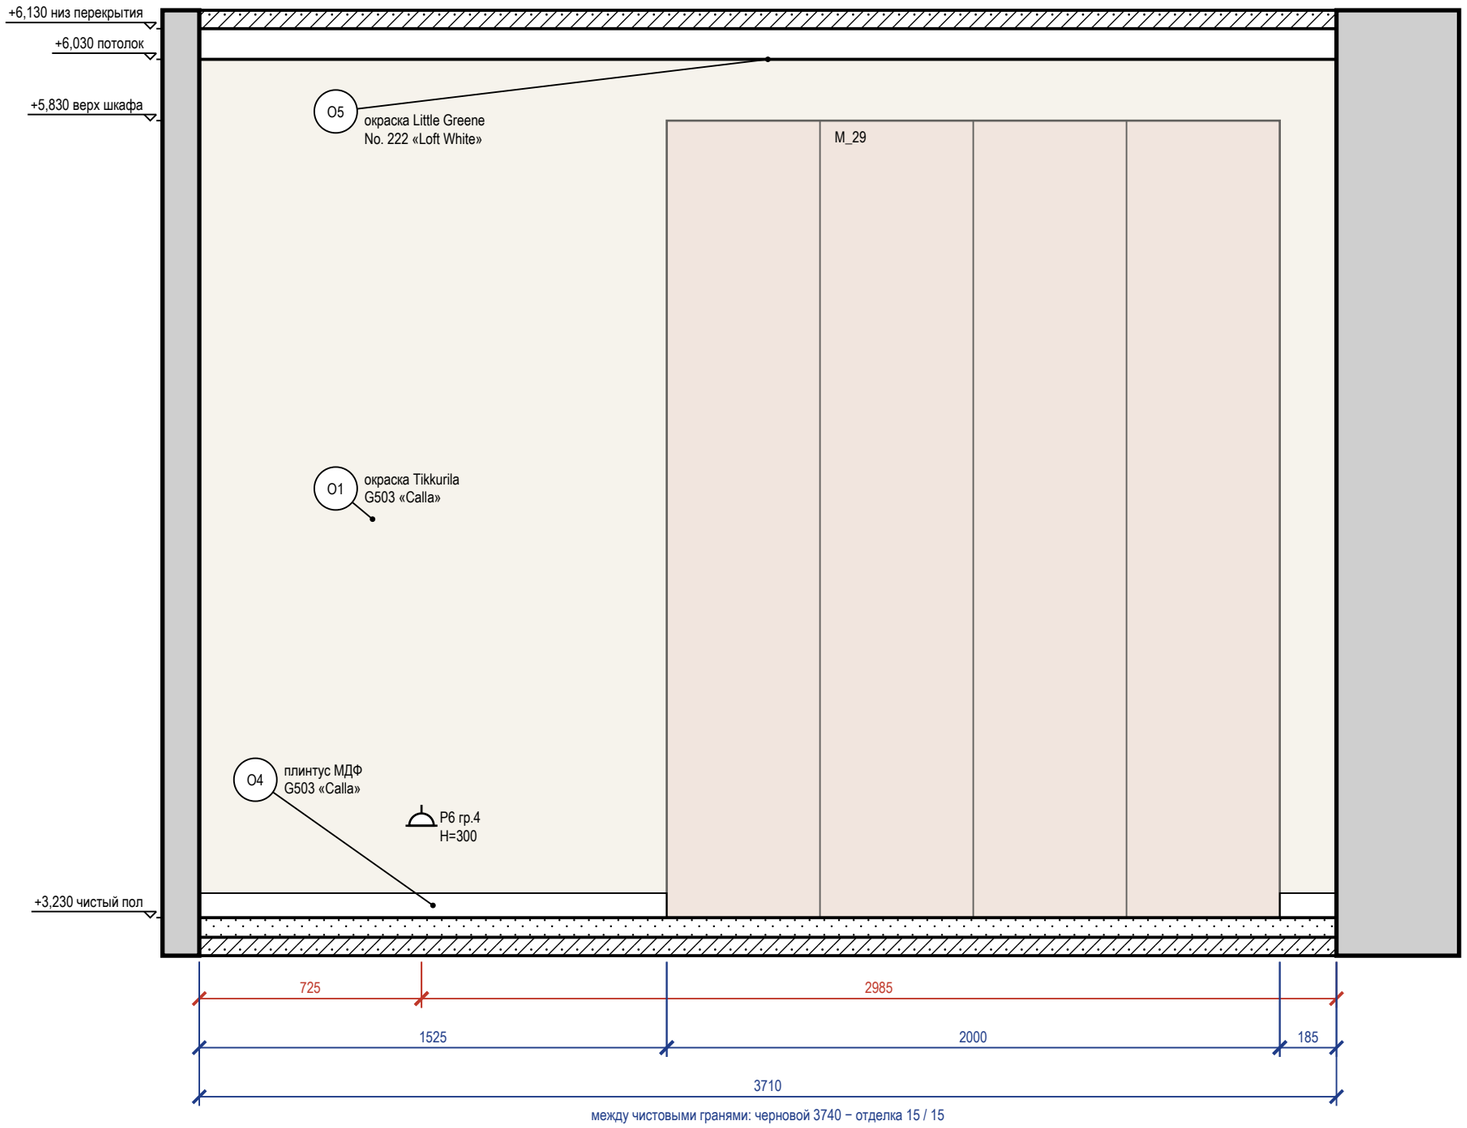


Схема развёрток (М 1:100)

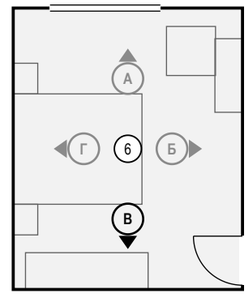


Ведомость отделки (на листе)

Марка	Поверхность	Материал, изделие	Цвет, код	Кол.
О1	стены	окраска, Tikkurila, матовая, подготовка Q3	Tikkurila G503 «Calla»	10,4 м²
О4	плинтус	плинтус МДФ, h 80 мм, аналог: плинтус МДФ под покраску 80×16	Tikkurila G503 «Calla»	1,7 м
О5	потолок	окраска, Little Greene Absolute Matt, глубокоматовая, подготовка Q3	Little Greene No. 222 «Loft White»	17,2 м²

5 **Плинтус МДФ 80×16 мм у окрашенной стены по доске (ламинату) (М 1:20)**

Узел 5 — лист С8

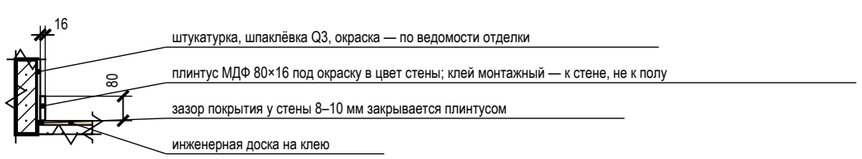

Примечания

1. Размеры — в мм от чистовых поверхностей стен; условные обозначения и общие указания — лист 3.
2. Потолок — у каждой стены свой, по плану потолков (ПТ7); ступени — зоной, кромка короба перед нишей — тонкой линией; в поле потолка: ПТ6 +5,880.

					Проект: Дом 120 м² — М 1:20
	Лист	№ док.	Подпись	Дата	Развёртка стены В. Спальня родителей (пом. 6)
Дизайнер	Кырлан А.С.			04.11.26	

Стадия	Лист	Листов
П	93	136

выпуск 04.11.2026 № 406ed8a6ce · стр. 93 из 136

Развёртка стены Г


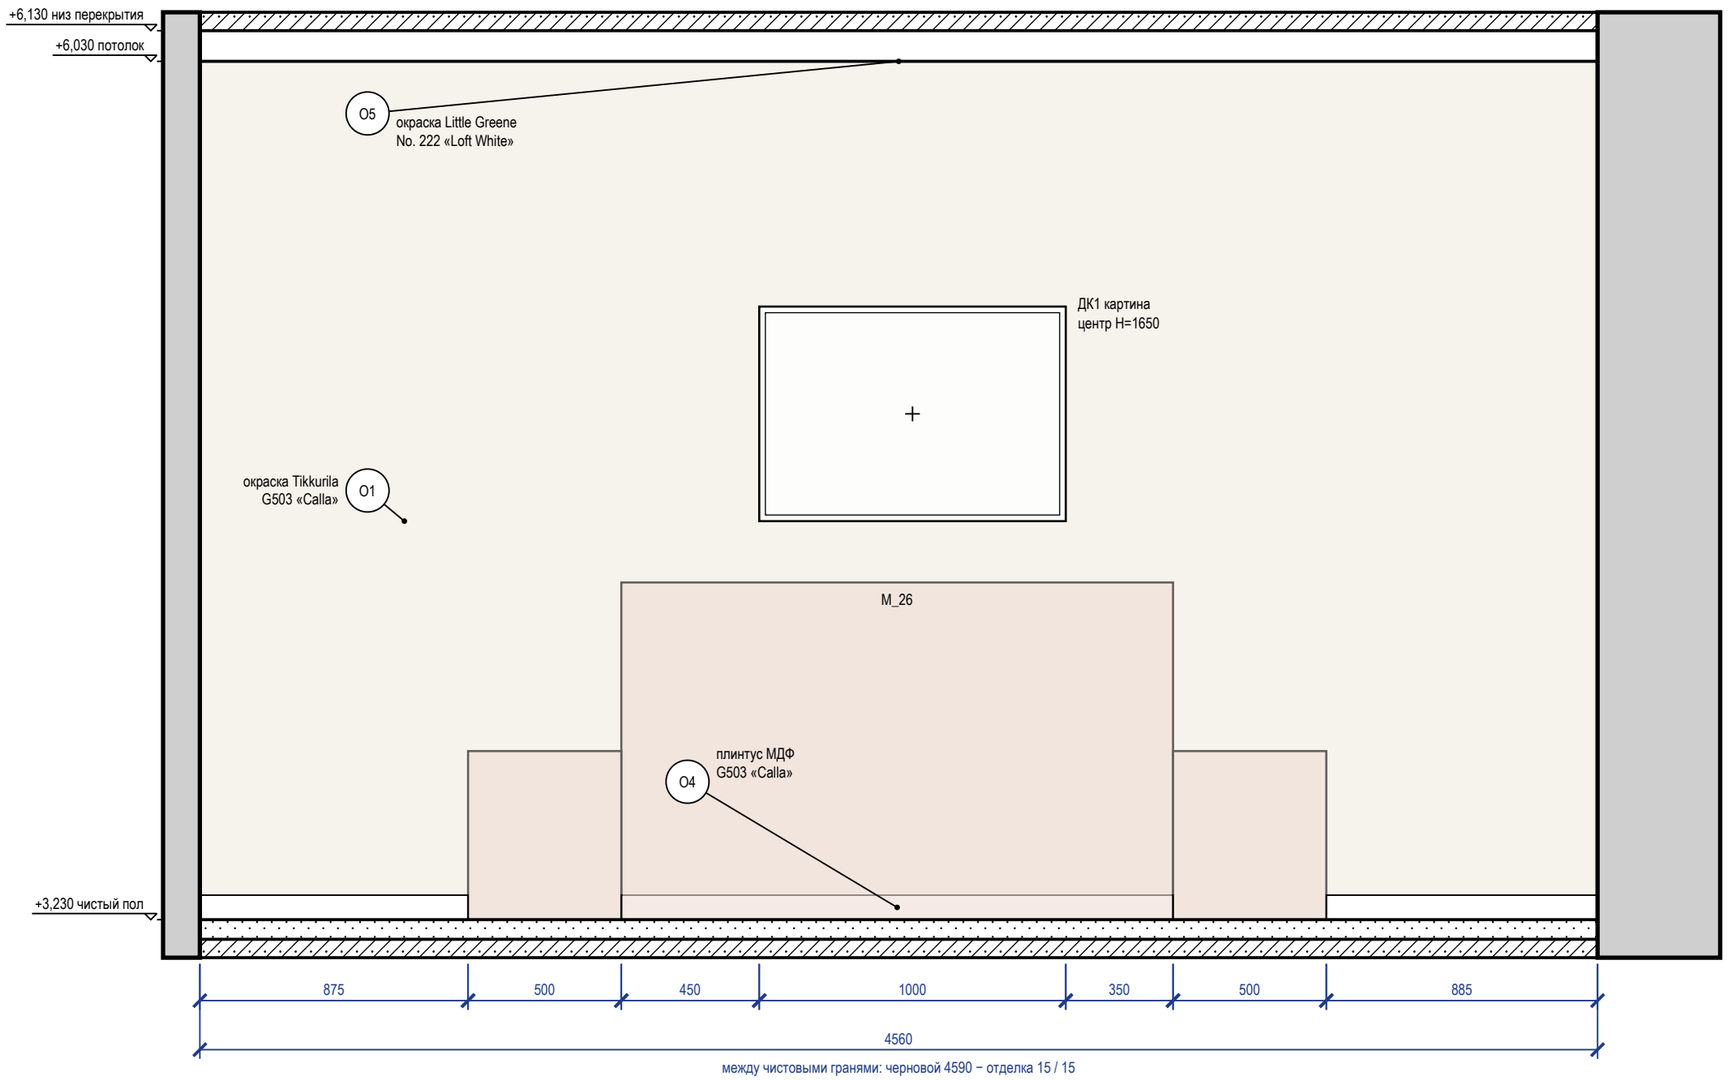


Схема развёрток (М 1:100)

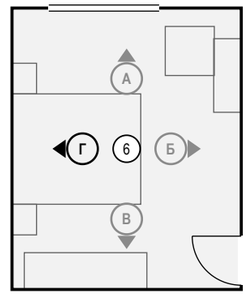

Ведомость отделки (на листе)

Марка	Поверхность	Материал, изделие	Цвет, код	Кол.
О1	стены	окраска, Tikkurila, матовая, подготовка Q3	Tikkurila G503 «Calla»	12,8 м²
О4	плинтус	плинтус МДФ, h 80 мм, аналог: плинтус МДФ под покраску 80×16	Tikkurila G503 «Calla»	3,6 м
О5	потолок	окраска, Little Greene Absolute Matt, глубокоматовая, подготовка Q3	Little Greene No. 222 «Loft White»	17,2 м²

Примечания

1. Размеры — в мм от чистовых поверхностей стен; условные обозначения и общие указания — лист 3.
2. Стена Г показана двумя видами: здесь — архитектурная развёртка (мебель, отделка, проёмы, высоты), электроточки и выводы ВК с привязками и таблицей — на листе 95 («Привязки»).
3. Картины и зеркала крепить к основанию по паспорту изделия (закладные и анкеры — в перечне скрытых работ); крест — ось центра предмета.
4. Потолок — у каждой стены свой, по плану потолков (ПТ7); ступени — зоной, кромка короба перед нишей — тонкой линией; в поле потолка: ПТ6 +5,880.

	Лист	№ док.	Подпись	Дата
Дизайнер	Кырлан А.С.			04.11.26

Проект: Дом 120 м² — **М 1:20**

Развёртка стены Г. Спальня родителей (пом. 6)

Стадия	Лист	Листов
П	94	136

Развёртка стены Г: электроточки и выводы

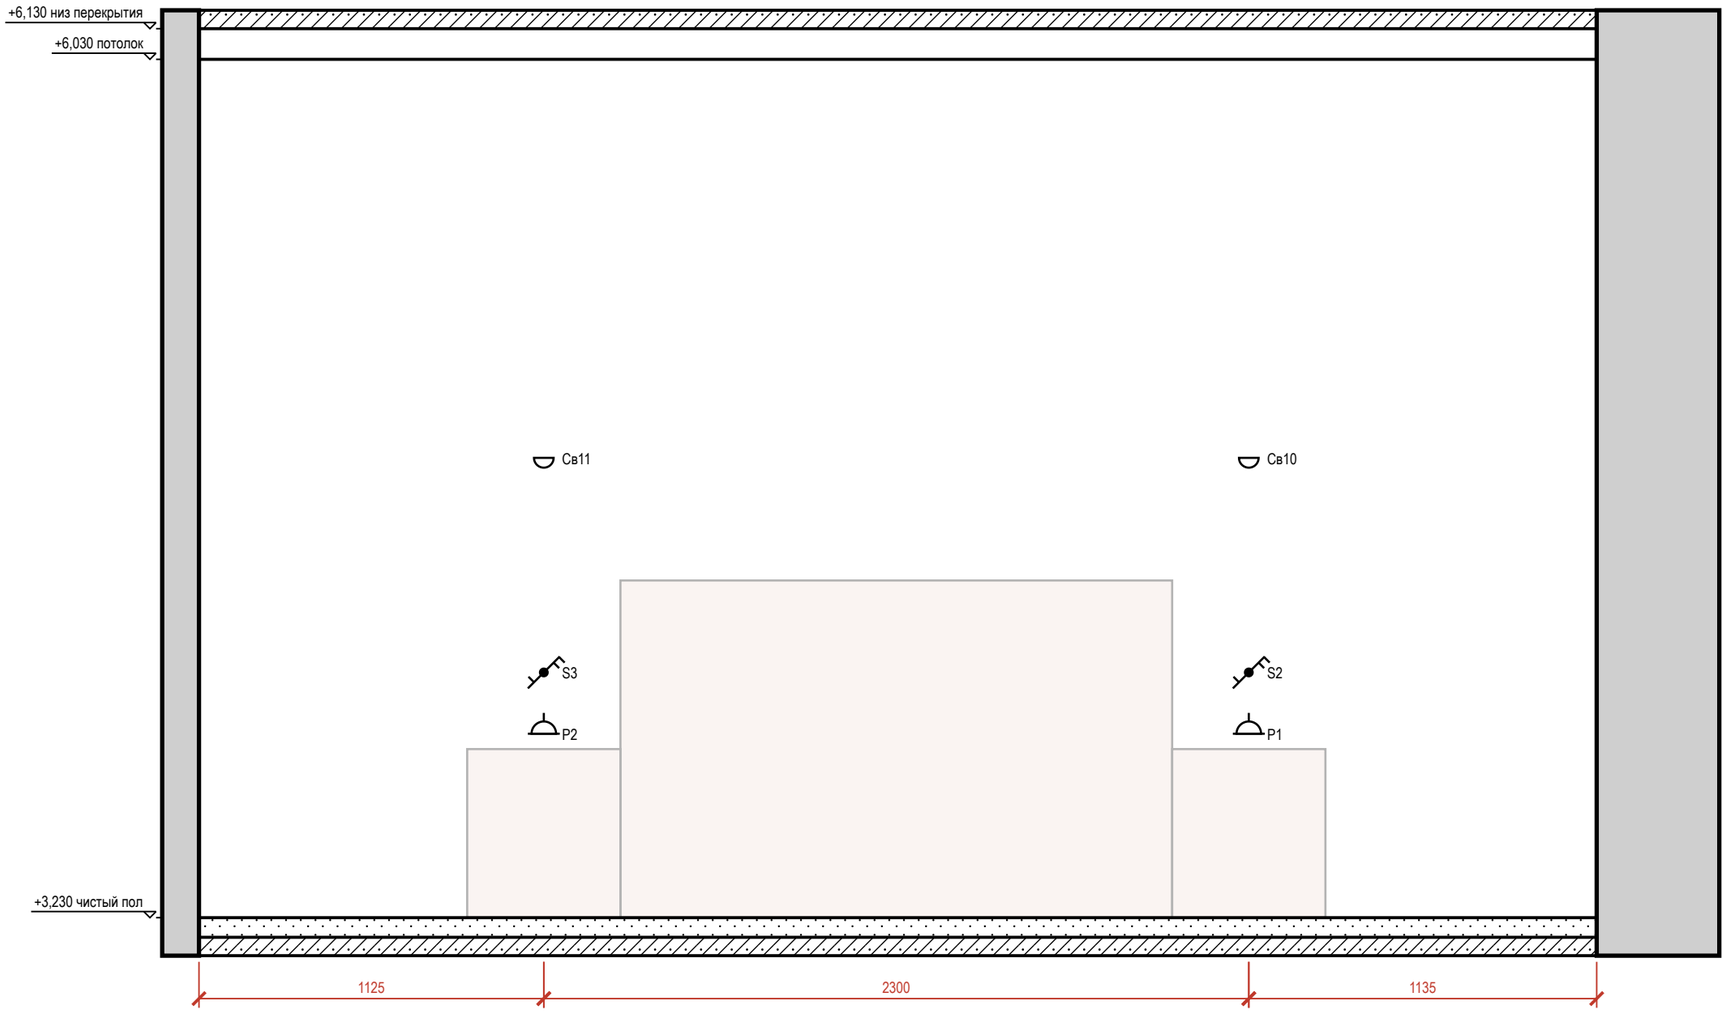



Таблица привязок электроточек и выводов

Марка	Назначение	От угла, мм	H от пола, мм	Примечание
P2	розетка: у кровати	1125	600	гр. 4
S3	выключатель	1125	800	гр. 1
Св11	светильник настенный	1125	1500	гр. 1
P1	розетка: у кровати	3425	600	гр. 4
S2	выключатель	3425	800	гр. 1
Св10	светильник настенный	3425	1500	гр. 1

Условные обозначения

- розетка с заземляющим контактом; у знака — марка, ×N постов в рамке, гр. — группа щита, H — высота оси, мм
- выключатель одноклавишный
- выключатель двухклавишный (флажков — по числу клавиш)
- выключатель с проходной или перекрёстной клавишей (обратный флажок); тип клавиши — в подписи
- светильник настенный (бра), H — высота оси
- привязки точек и выводов от угла и от пола, мм
- марка развёртки: буква стены, стрелка — взгляд

Схема развёрток (М 1:200)

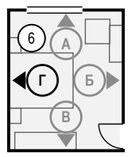

Примечания

1. Вид «Привязки» стены Г — электроточки и выводы ВК; архитектурная развёртка (мебель, отделка, проёмы, высоты) — на листе 94. Мебель и приборы — подложкой для ориентира; их марки и обозначения мебели, проёмов и стен — там же.
2. Привязки — в мм: по горизонтали от левого чистового угла стены до оси изделия, H — от чистого пола до оси; все точки — в таблице привязок. Красная цепочка — привязки по осям; точки ближе 120 мм одна к другой в цепочку не дробятся — их привязки только в таблице.
3. У знака — марка электроточки (P — розетка, S — выключатель, Св — светильник, ЭВ — вывод кабеля); условные обозначения и общие указания — лист 3.

					Проект: Дом 120 м²	М 1:20
	Лист	№ док.	Подпись	Дата	Привязки электроточек, стена Г. Спальня родителей (пом. 6)	Стадия: П; Лист: 95; Листов: 136
Дизайнер	Кырлан А.С.			04.11.26		

Развёртка стены А


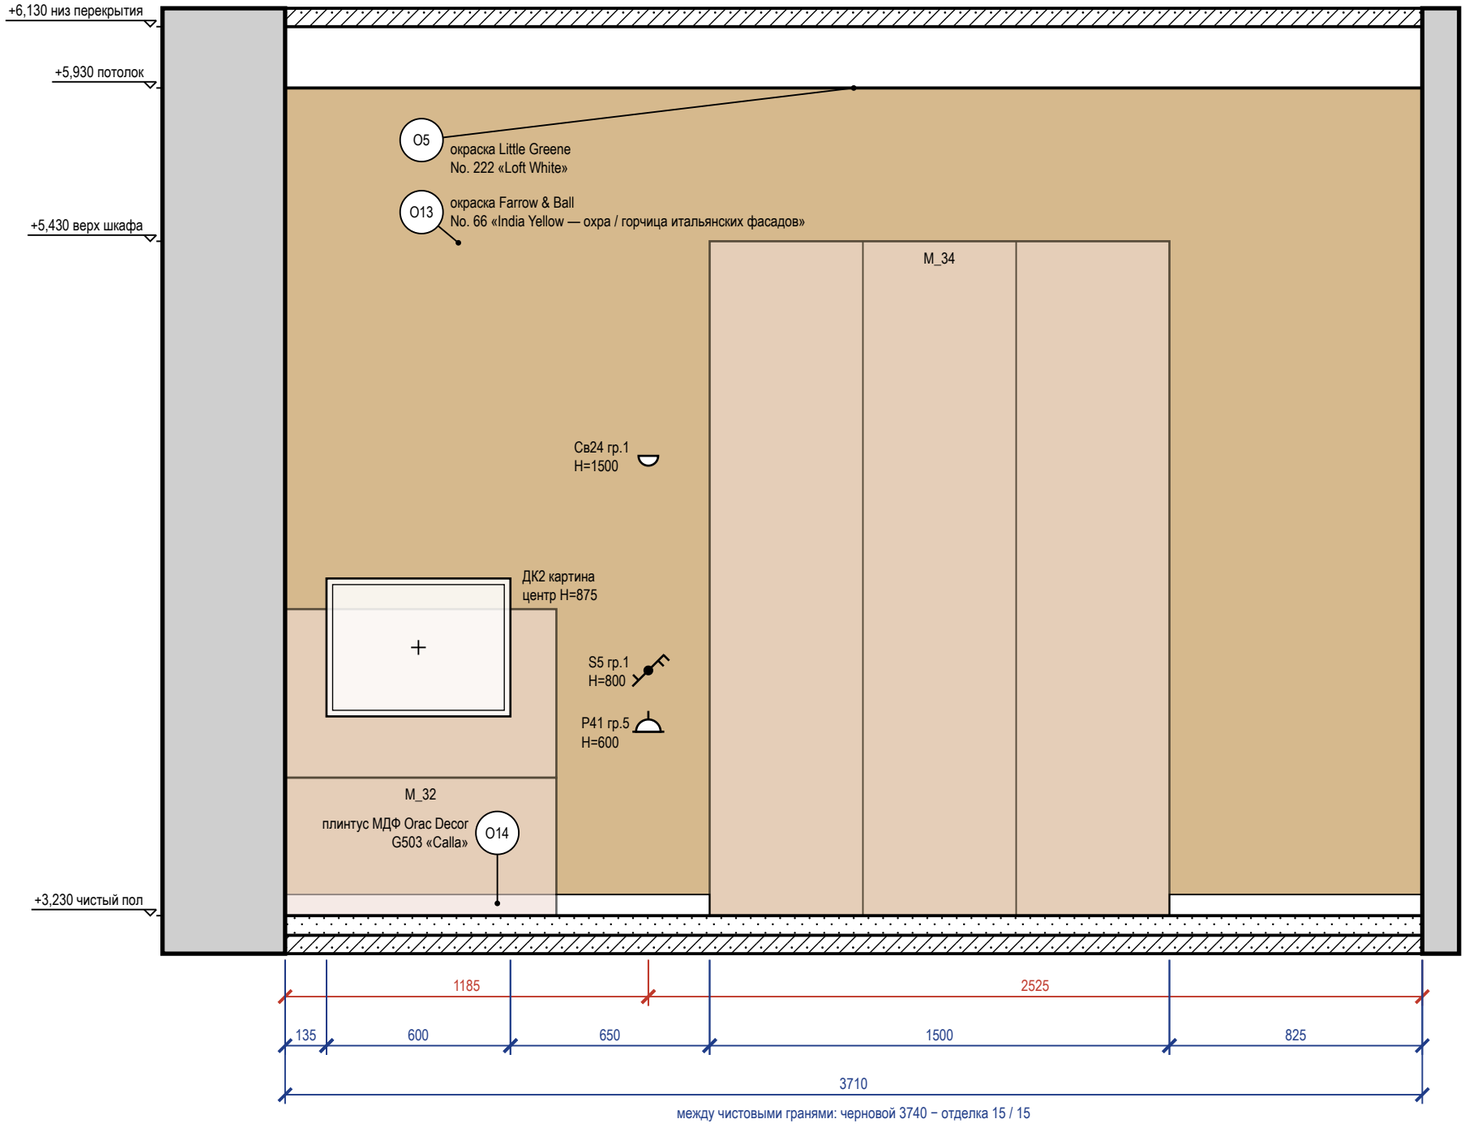


Схема развёрток (М 1:100)

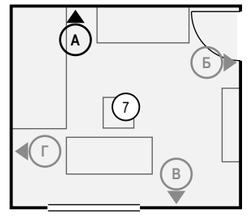

Ведомость отделки (на листе)

Марка	Поверхность	Материал, изделие	Цвет, код	Кол.
O5	потолок	окраска, Little Greene Absolute Matt, глубокоматовая, подготовка Q3	Little Greene No. 222 «Loft White»	12,3 м²
O13	акцентная стена	окраска, Farrow & Ball, шелковисто-матовая, подготовка Q3	Farrow & Ball No. 66 «India Yellow — охра / горчица итальянских фасадов»	10 м²
O14	плинтус	плинтус МДФ, Orac Decor Contour (Luxxus), h 69 мм, SX165	Tikkurila G503 «Calla»	2,2 м

Примечания

1. Размеры — в мм от чистовых поверхностей стен; условные обозначения и общие указания — лист 3.
2. Картины и зеркала крепить к основанию по паспорту изделия (закладные и анкеры — в перечне скрытых работ); крест — ось центра предмета.
3. Потолок — у каждой стены свой, по плану потолков (ПТ8); ступени — зоной, кромка короба перед нишей — тонкой линией; в поле потолка: ПТ7 +6,030.

					Проект: Дом 120 м²	М 1:20
	Лист	№ док.	Подпись	Дата		
Дизайнер	Кырлан А.С.			04.11.26	Развёртка стены А. Детская (пом. 7)	

Стадия	Лист	Листов
П	96	136

Развёртка стены Б


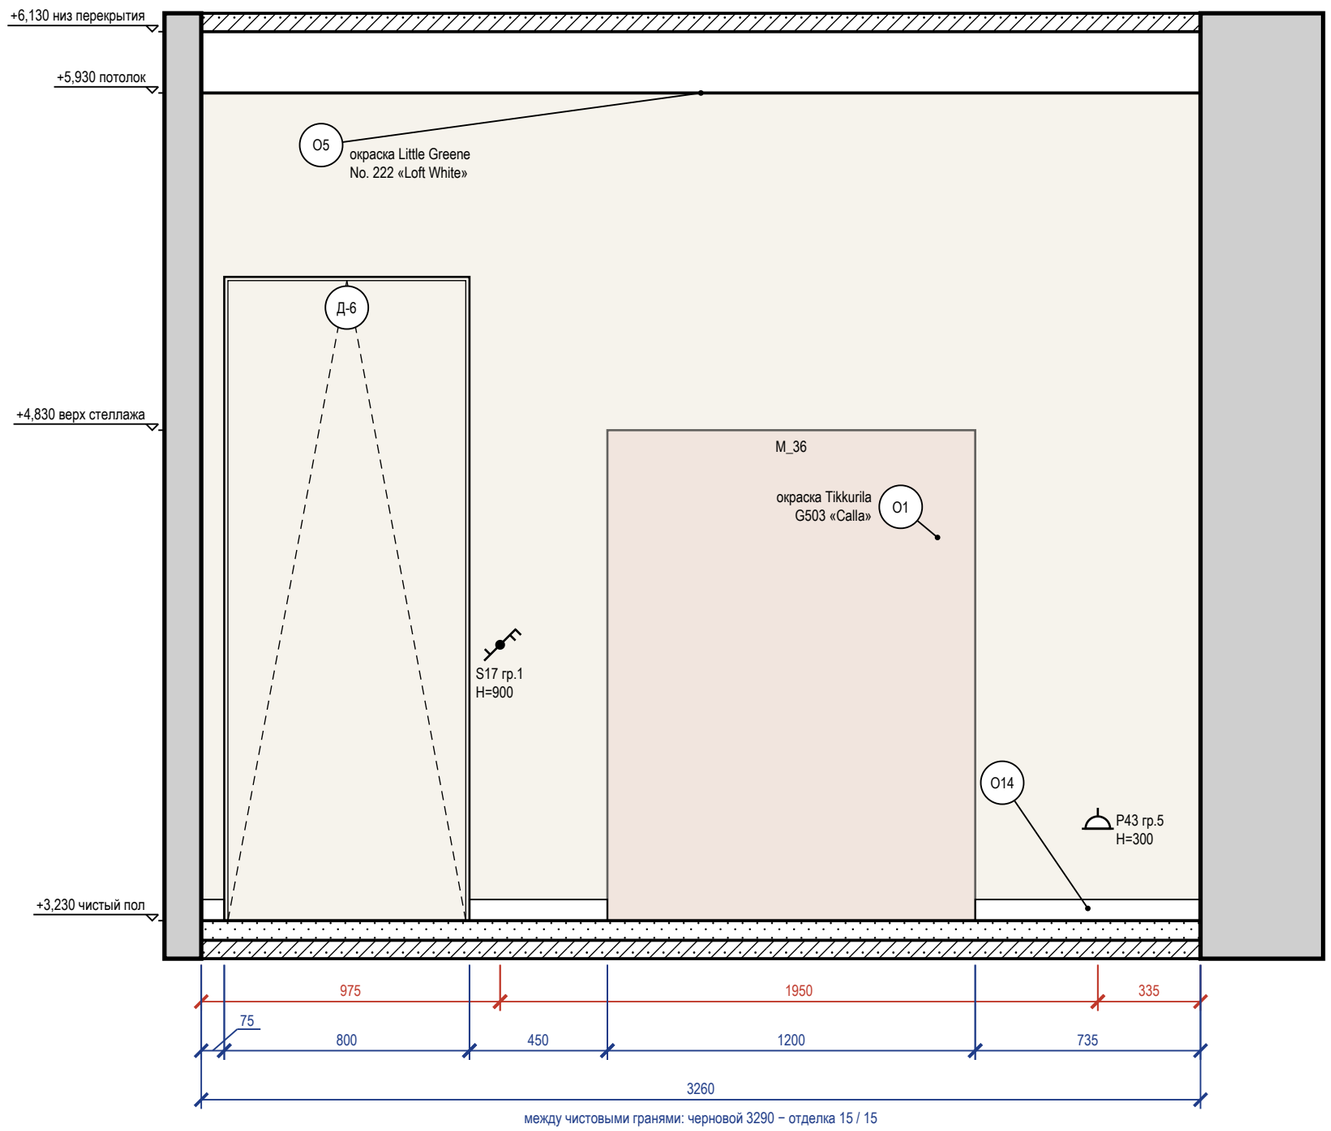


Схема развёрток (М 1:100)

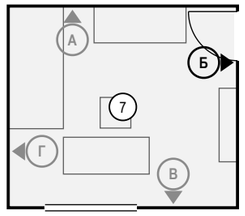

Ведомость отделки (на листе)

Марка	Поверхность	Материал, изделие	Цвет, код	Кол.
О1	стены	окраска, Tikkurila, шелковисто-матовая, подготовка Q3	Tikkurila G503 «Calla»	7,1 м²
О5	потолок	окраска, Little Greene Absolute Matt, глубокоматовая, подготовка Q3	Little Greene No. 222 «Loft White»	12,3 м²
О14	плинтус	плинтус МДФ, Orac Decor Contour (Luxxus), h 69 мм, SX165	Tikkurila G503 «Calla»	1,3 м

Примечания

1. Размеры — в мм от чистовых поверхностей стен; условные обозначения и общие указания — лист 3.
2. Двери скрытого монтажа — полотно в плоскости стены, отделка стены по полотну, плинтус прерывается у короба (узел — на листе узлов).
3. Потолок — у каждой стены свой, по плану потолков (ПТ8); ступени — зоной, кромка короба перед нишей — тонкой линией; в поле потолка: ПТ7 +6,030.

					Проект: Дом 120 м² — М 1:20
	Лист	№ док.	Подпись	Дата	Развёртка стены Б. Детская (пом. 7)
Дизайнер	Кырлан А.С.			04.11.26	

Стадия	Лист	Листов
П	97	136

Развёртка стены В


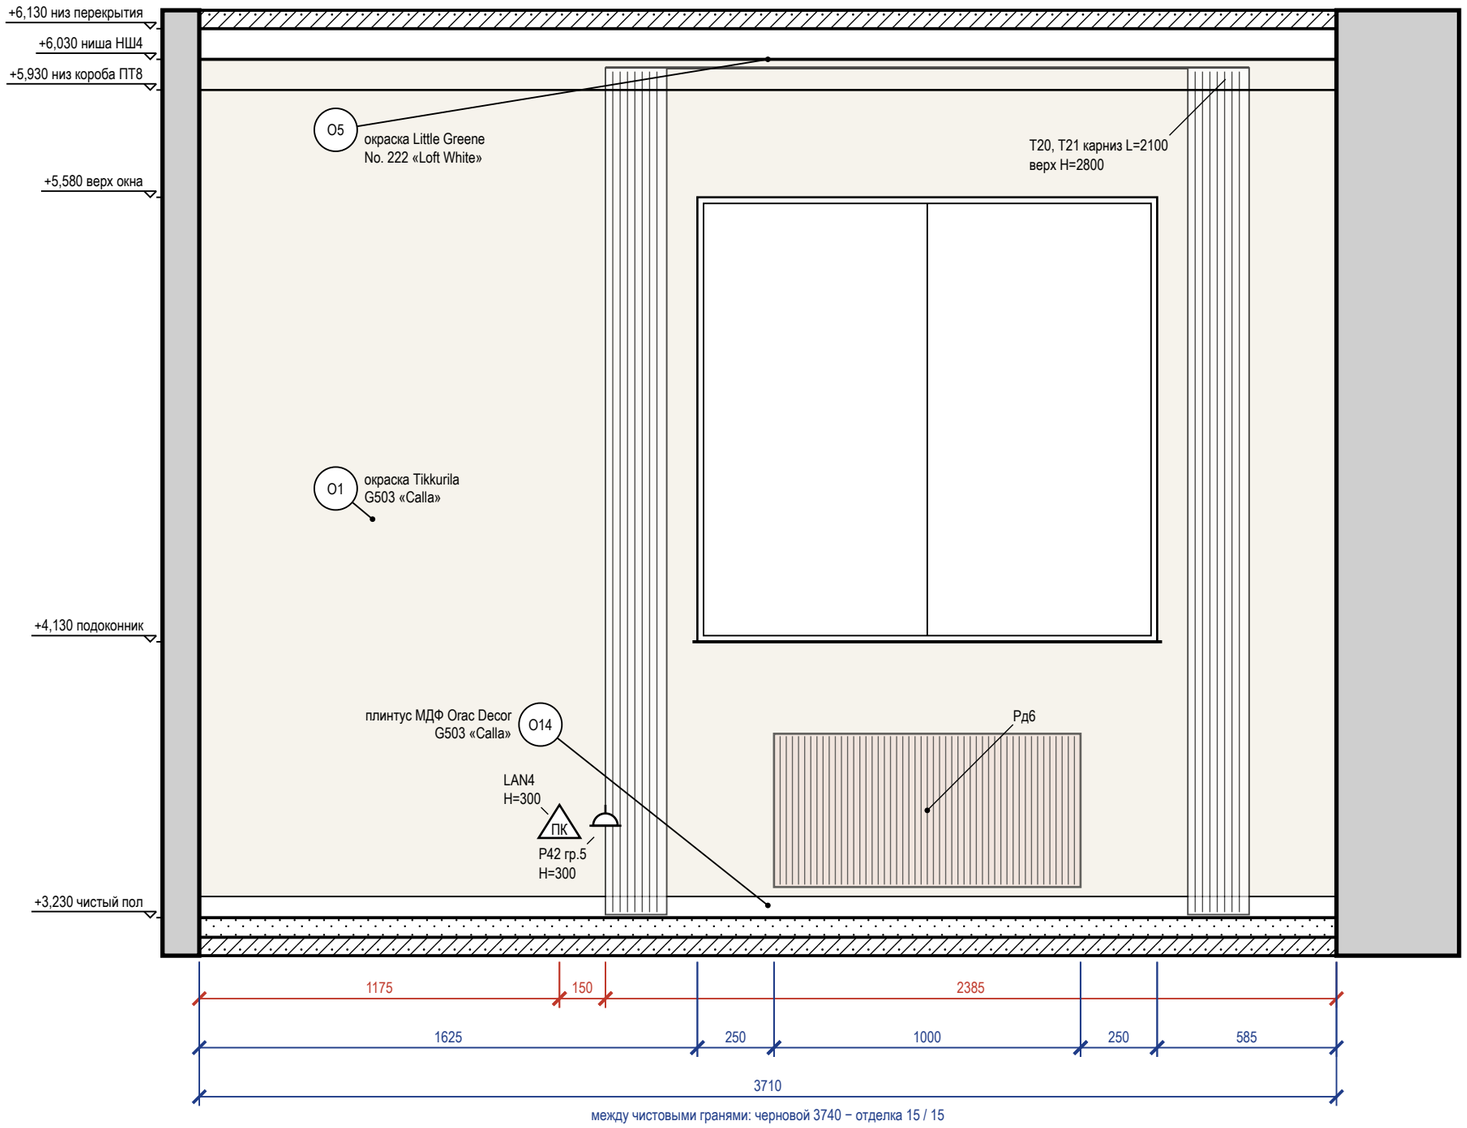


Схема развёрток (М 1:100)

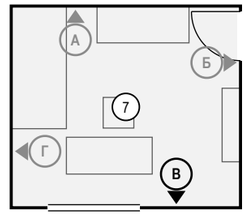

Ведомость отделки (на листе)

Марка	Поверхность	Материал, изделие	Цвет, код	Кол.
О1	стены	окраска, Tikkurila, шелковисто-матовая, подготовка Q3	Tikkurila G503 «Calla»	8,2 м²
О5	потолок	окраска, Little Greene Absolute Matt, глубокоматовая, подготовка Q3	Little Greene No. 222 «Loft White»	12,3 м²
О14	плинтус	плинтус МДФ, Orac Decor Contour (Luxxus), h 69 мм, SX165	Tikkurila G503 «Calla»	3,7 м

Примечания

1. Размеры — в мм от чистовых поверхностей стен; условные обозначения и общие указания — лист 3.
2. Карнизы (шины) — по ведомости текстиля декоратора: длина L и верх H на развёртке — те же числа, что в ведомости; крепление — до окраски потолка.
3. Потолок — у каждой стены свой, по плану потолков (НШ4, ПТ8); ступени — зоной, кромка короба перед нишей — тонкой линией; в поле потолка: ПТ7 +6,030.

					Проект: Дом 120 м²	М 1:20
	Лист	№ док.	Подпись	Дата	Развёртка стены В. Детская (пом. 7)	Стадия / Лист / Листов
Дизайнер	Кырлан А.С.			04.11.26		П / 98 / 136

Развёртка стены Г


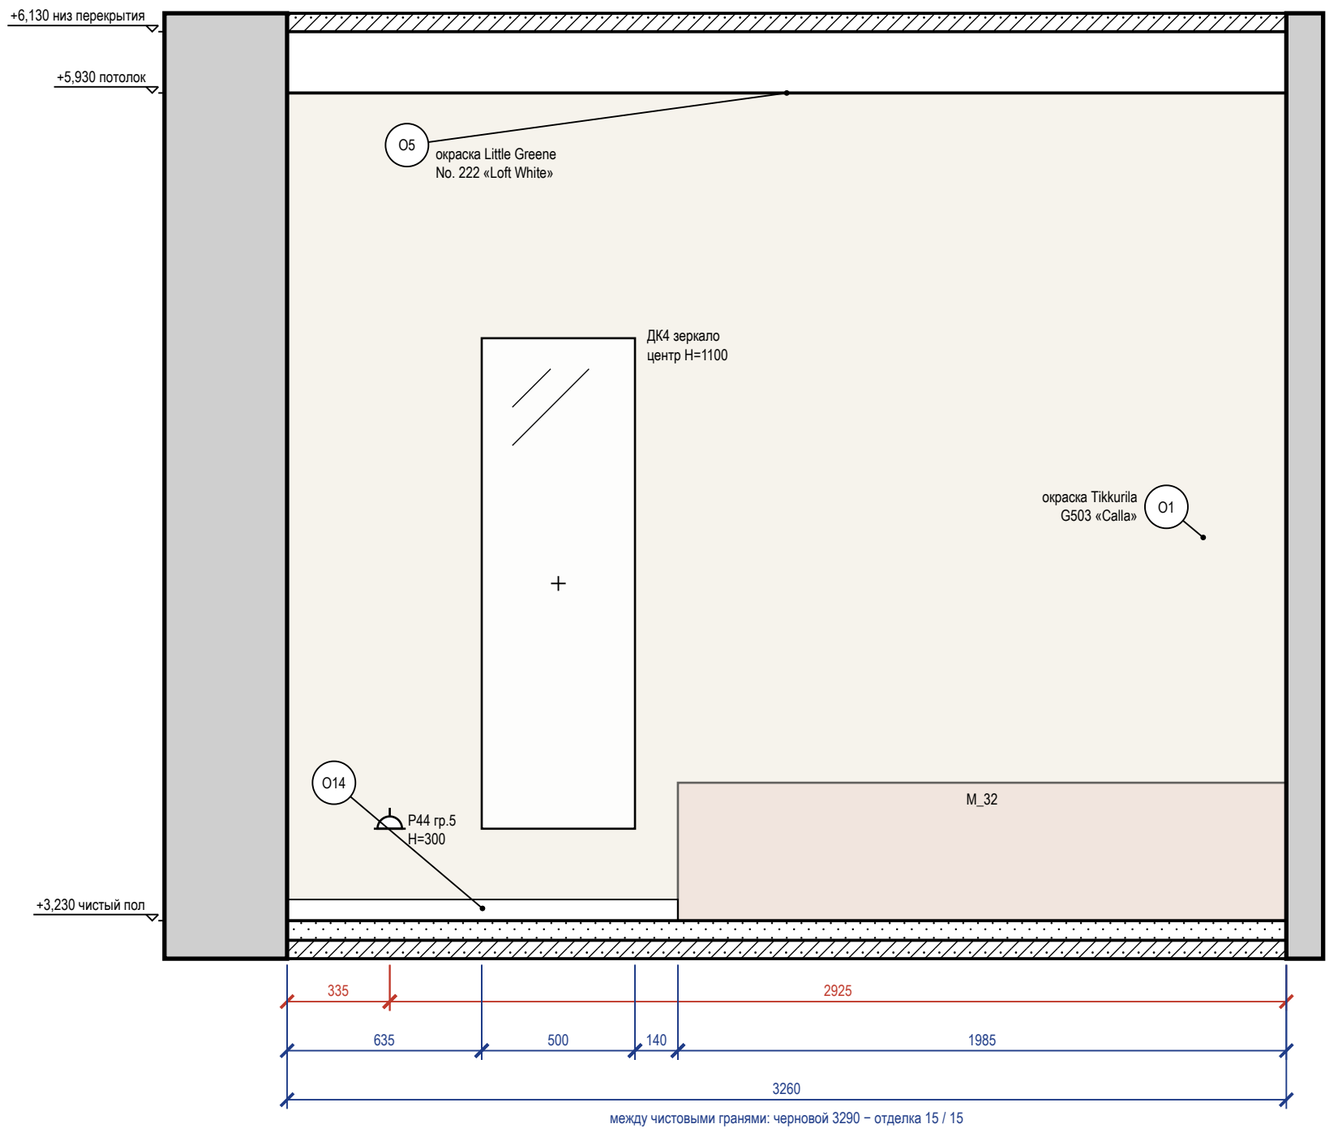


Схема развёрток (М 1:100)

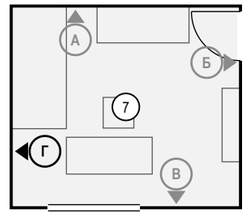

Ведомость отделки (на листе)


Марка	Поверхность	Материал, изделие	Цвет, код	Кол.
О1	стены	окраска, Tikkurila, шелковисто-матовая, подготовка Q3	Tikkurila G503 «Calla»	8,8 м²
О5	потолок	окраска, Little Greene Absolute Matt, глубокоматовая, подготовка Q3	Little Greene No. 222 «Loft White»	12,3 м²
О14	плинтус	плинтус МДФ, Orac Decor Contour (Luxxus), h 69 мм, SX165	Tikkurila G503 «Calla»	1,3 м

Примечания

1. Размеры — в мм от чистовых поверхностей стен; условные обозначения и общие указания — лист 3.
2. Картины и зеркала крепить к основанию по паспорту изделия (закладные и анкеры — в перечне скрытых работ); крест — ось центра предмета.
3. Потолок — у каждой стены свой, по плану потолков (ПТ8); ступени — зоной, кромка короба перед нишей — тонкой линией; в поле потолка: ПТ7 +6,030.


					Проект: Дом 120 м²	М 1:20
	Лист	№ док.	Подпись	Дата		
Дизайнер	Кырлан А.С.			04.11.26	Развёртка стены Г. Детская (пом. 7)	
					Стадия: П	Лист: 99 / Листов: 136

Развёртка стены А

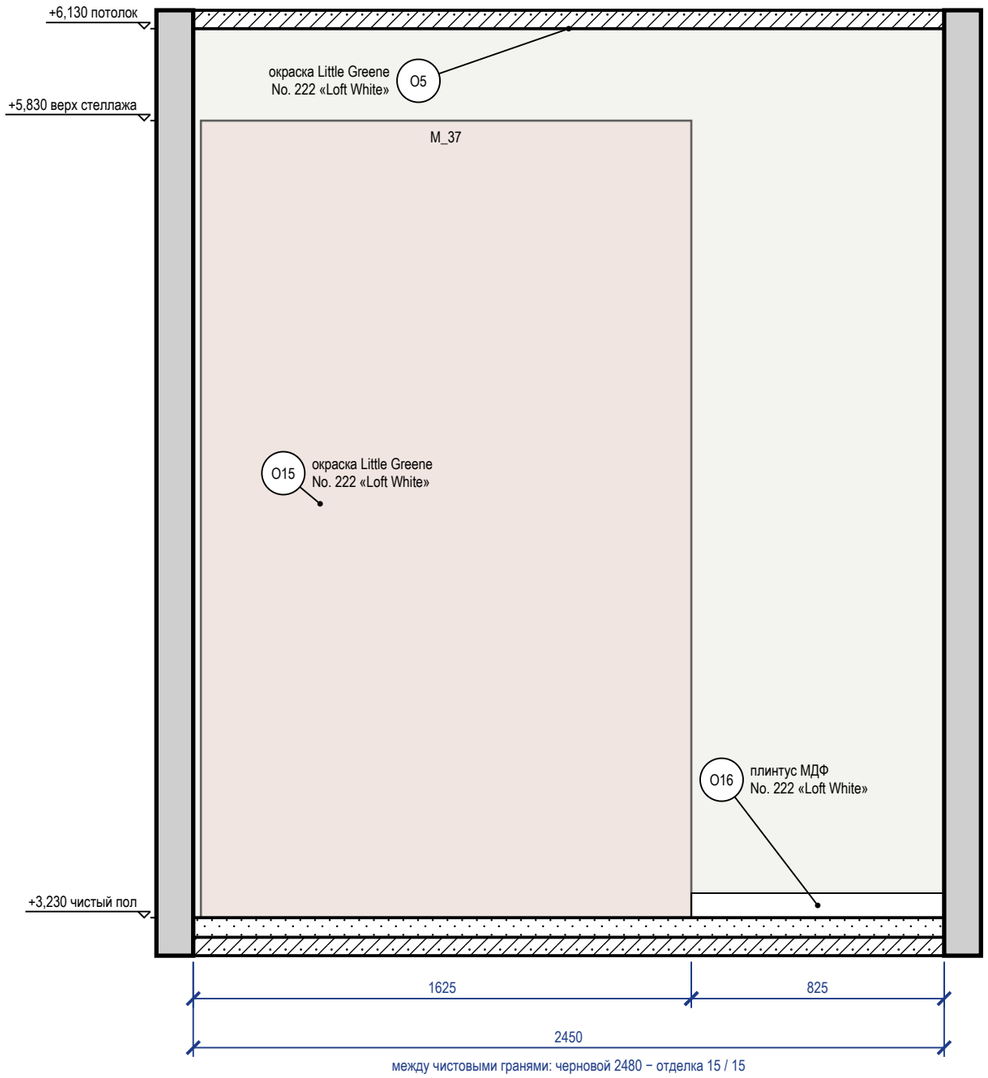


между чистовыми гранями: черновой 2480 − отделка 15 / 15

Развёртка стены Б

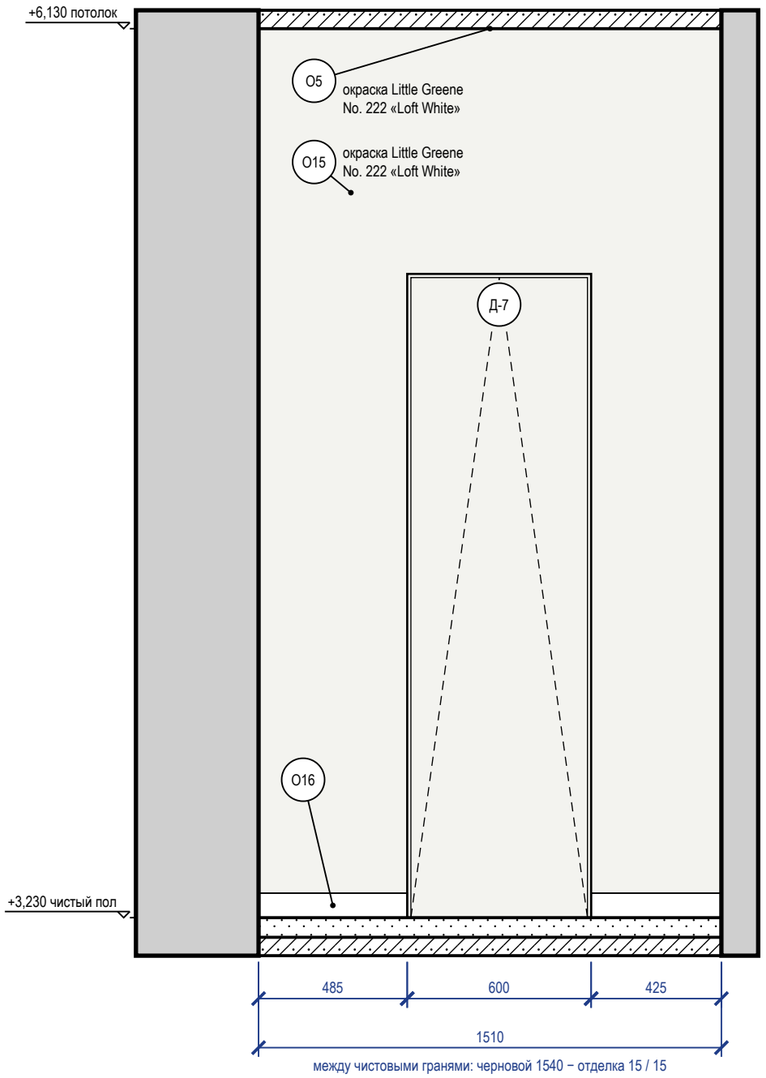

между чистовыми гранями: черновой 1540 − отделка 15 / 15

Схема развёрток (М 1:100)

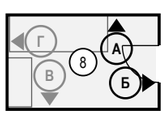

Ведомость отделки (на листе)


Марка	Поверхность	Материал, изделие	Цвет, код	Кол.
O5	потолок	окраска, Little Greene Absolute Matt, глубокоматовая, подготовка Q3	Little Greene No. 222 «Loft White»	3,8 м²
O15	стены	окраска, Little Greene Intelligent Matt, матовая, подготовка Q3	Little Greene No. 222 «Loft White»	10,2 м²
O16	плинтус	плинтус МДФ, h 80 мм, аналог: плинтус МДФ под покраску 80×16	Little Greene No. 222 «Loft White»	1,7 м

Примечания

1. Размеры — в мм от чистовых поверхностей стен; условные обозначения и общие указания — лист 3.
2. Двери скрытого монтажа — полотно в плоскости стены, отделка стены по полотну, плинтус прерывается у короба (узел — на листе узлов).

					Проект: Дом 120 м² — М 1:20
	Лист	№ док.	Подпись	Дата	Развёртки стен А, Б. Гардеробная (пом. 8)
Дизайнер	Кырлан А.С.			04.11.26	Стадия: П; Лист: 100; Листов: 136

Развёртка стены В

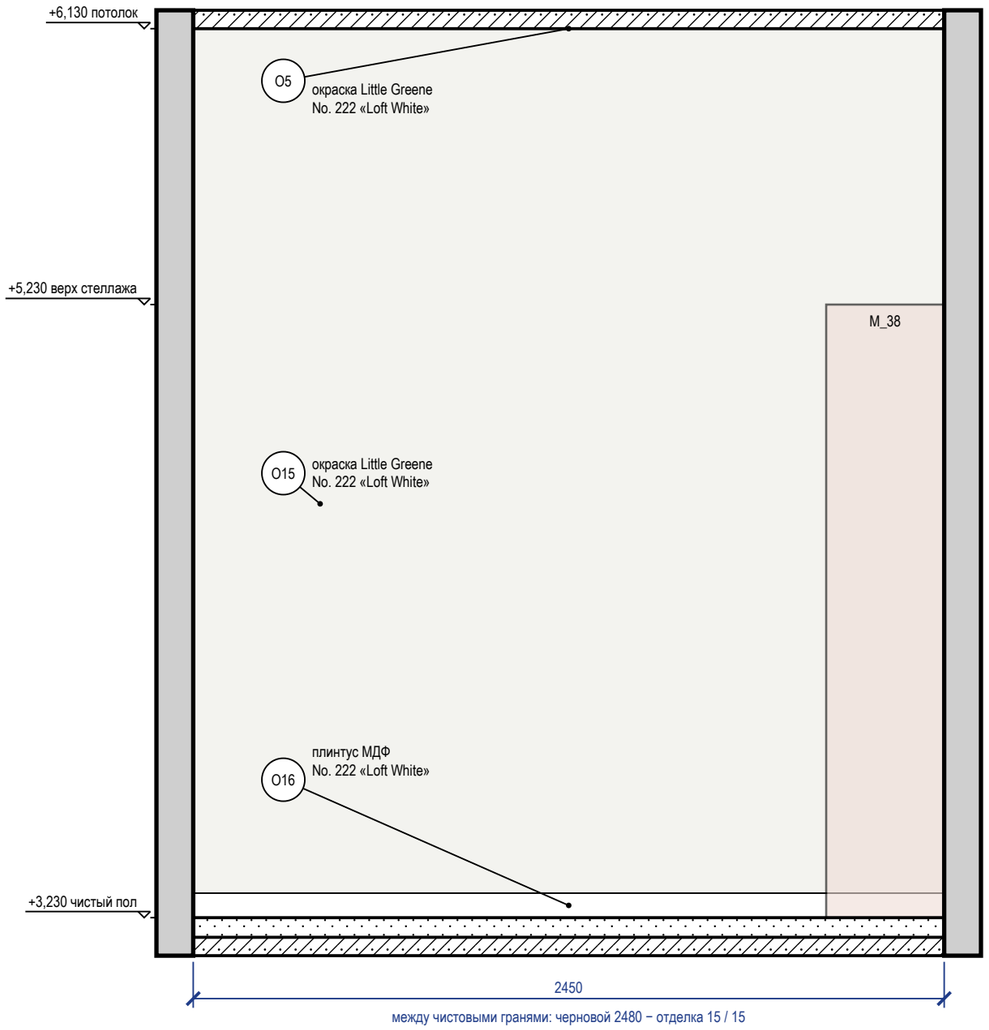

Развёртка стены Г


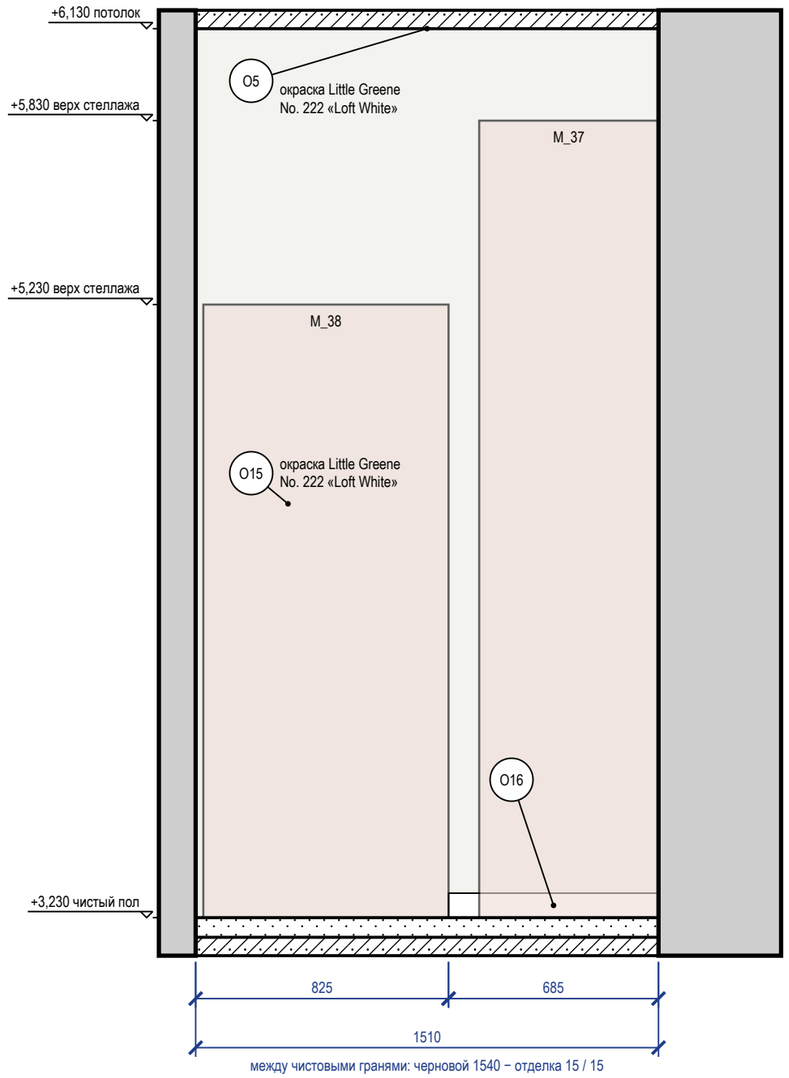


Схема развёрток (М 1:100)

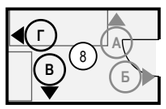

Ведомость отделки (на листе)

Марка	Поверхность	Материал, изделие	Цвет, код	Кол.
O5	потолок	окраска, Little Greene Absolute Matt, глубокоматовая, подготовка Q3	Little Greene No. 222 «Loft White»	3,8 м²
O15	стены	окраска, Little Greene Intelligent Matt, матовая, подготовка Q3	Little Greene No. 222 «Loft White»	11,5 м²
O16	плинтус	плинтус МДФ, h 80 мм, аналог: плинтус МДФ под покраску 80×16	Little Greene No. 222 «Loft White»	3,1 м

Примечания

1. Размеры — в мм от чистовых поверхностей стен; условные обозначения и общие указания — лист 3.

	Лист	№ док.	Подпись	Дата
Дизайнер	Кырлан А.С.			04.11.26


Проект: Дом 120 м² — **М 1:20**

Развёртки стен В, Г. Гардеробная (пом. 8)

Стадия	Лист	Листов
П	101	136


выпуск 04.11.2026 № 406ed8a6ce · стр. 101 из 136

Развёртка стены Б

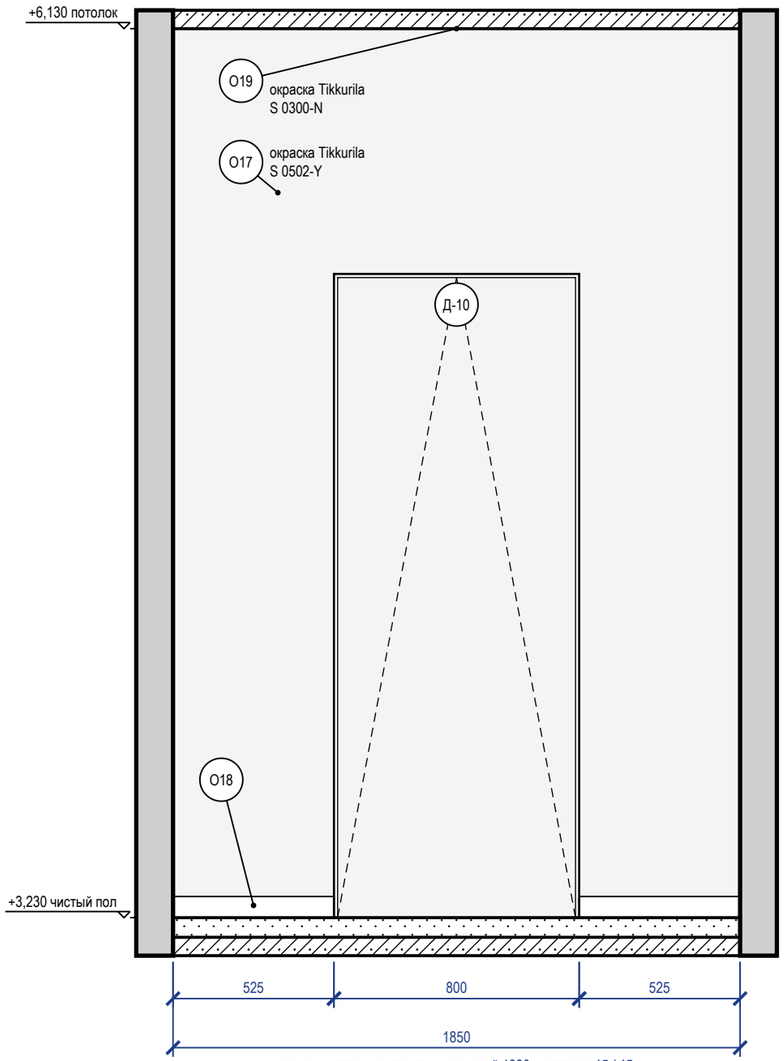


между чистовыми гранями: черновой 1880 − отделка 15 / 15

Развёртка стены В

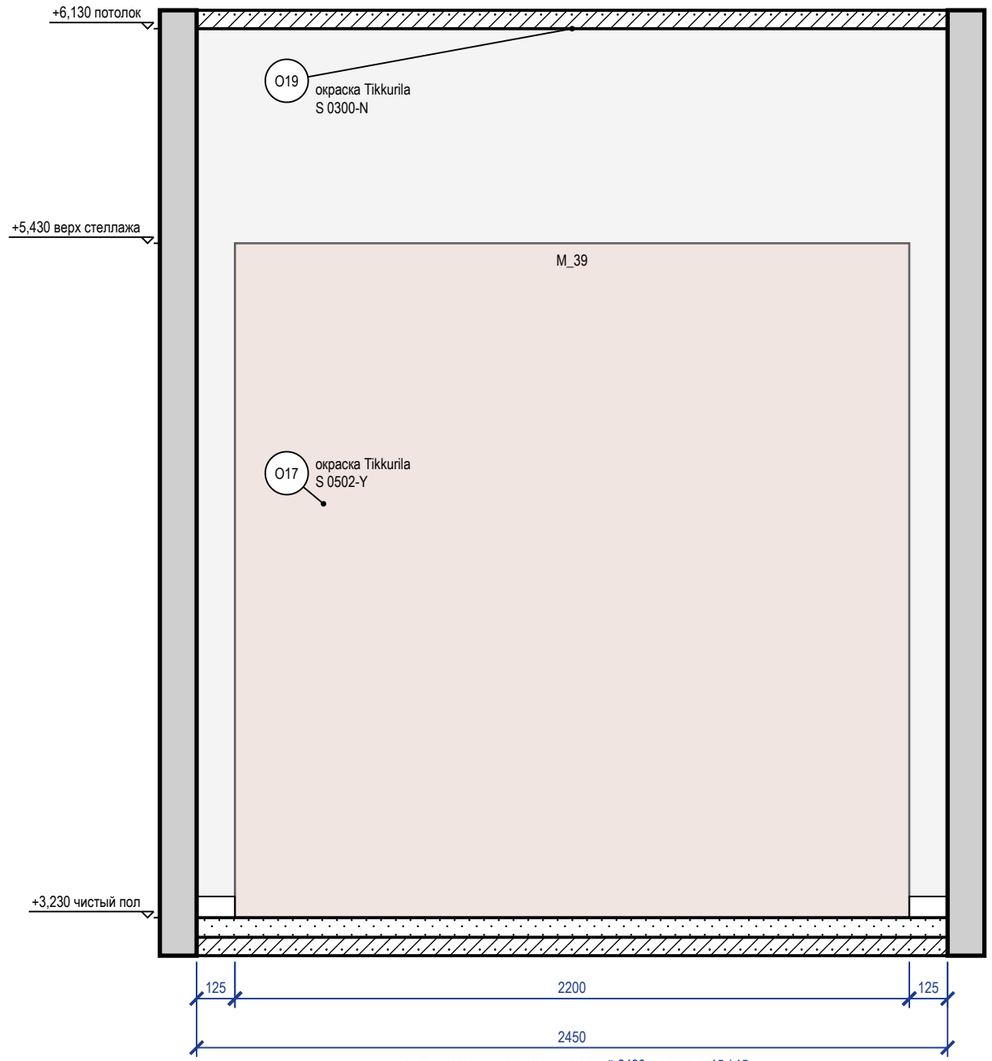

между чистовыми гранями: черновой 2480 − отделка 15 / 15

Схема развёрток (М 1:100)

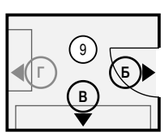

Ведомость отделки (на листе)

Марка	Поверхность	Материал, изделие	Цвет, код	Кол.
О17	стены	окраска, Tikkurila, матовая, подготовка Q3	NCS S 0502-Y	10,8 м²
О18	плинтус	плинтус МДФ, Orac Decor Contour (Luxxus), h 69 мм, SX165, шелковисто-матовая	NCS S 0300-N	1,3 м
О19	потолок	окраска, Tikkurila, глубокоматовая	NCS S 0300-N	4,7 м²

Примечания

1. Размеры — в мм от чистовых поверхностей стен; условные обозначения и общие указания — лист 3.
2. Двери скрытого монтажа — полотно в плоскости стены, отделка стены по полотну, плинтус прерывается у короба (узел — на листе узлов).

					Проект: Дом 120 м²	М 1:20
	Лист	№ док.	Подпись	Дата		
Дизайнер	Кырлан А.С.			04.11.26	Развёртки стен Б, В. Кладовая (пом. 9)	
					Стадия: П	Лист: 102 / Листов: 136

Развёртка стены Г


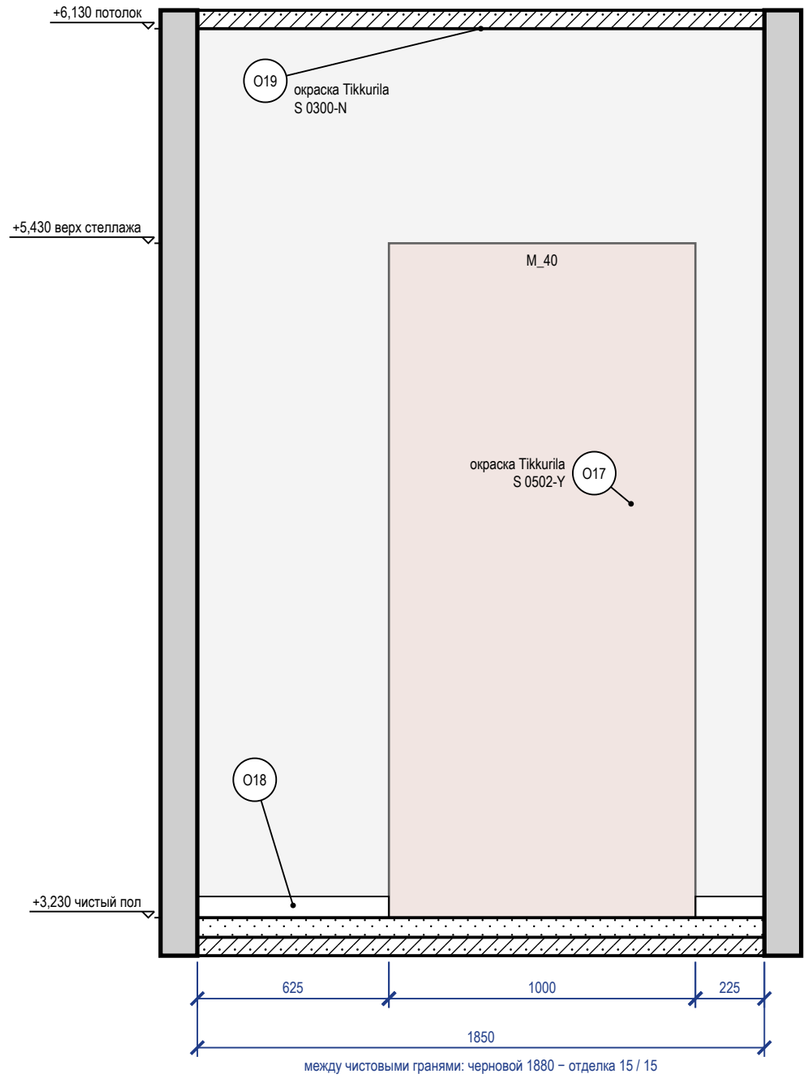


Схема развёрток (М 1:100)

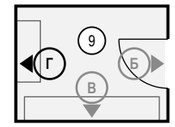

Ведомость отделки (на листе)

Марка	Поверхность	Материал, изделие	Цвет, код	Кол.
О17	стены	окраска, Tikkurila, матовая, подготовка Q3	NCS S 0502-Y	5,4 м²
О18	плинтус	плинтус МДФ, Orac Decor Contour (Luxxus), h 69 мм, SX165, шелковисто-матовая	NCS S 0300-N	0,8 м
О19	потолок	окраска, Tikkurila, глубокоматовая	NCS S 0300-N	4,7 м²

Примечания

1. Размеры — в мм от чистовых поверхностей стен; условные обозначения и общие указания — лист 3.

					Проект: Дом 120 м²	М 1:20
	Лист	№ док.	Подпись	Дата		
Дизайнер	Кырлан А.С.			04.11.26	Развёртка стены Г. Кладовая (пом. 9)	
					Стадия: П	Лист: 103 / Листов: 136

Развёртка стены А


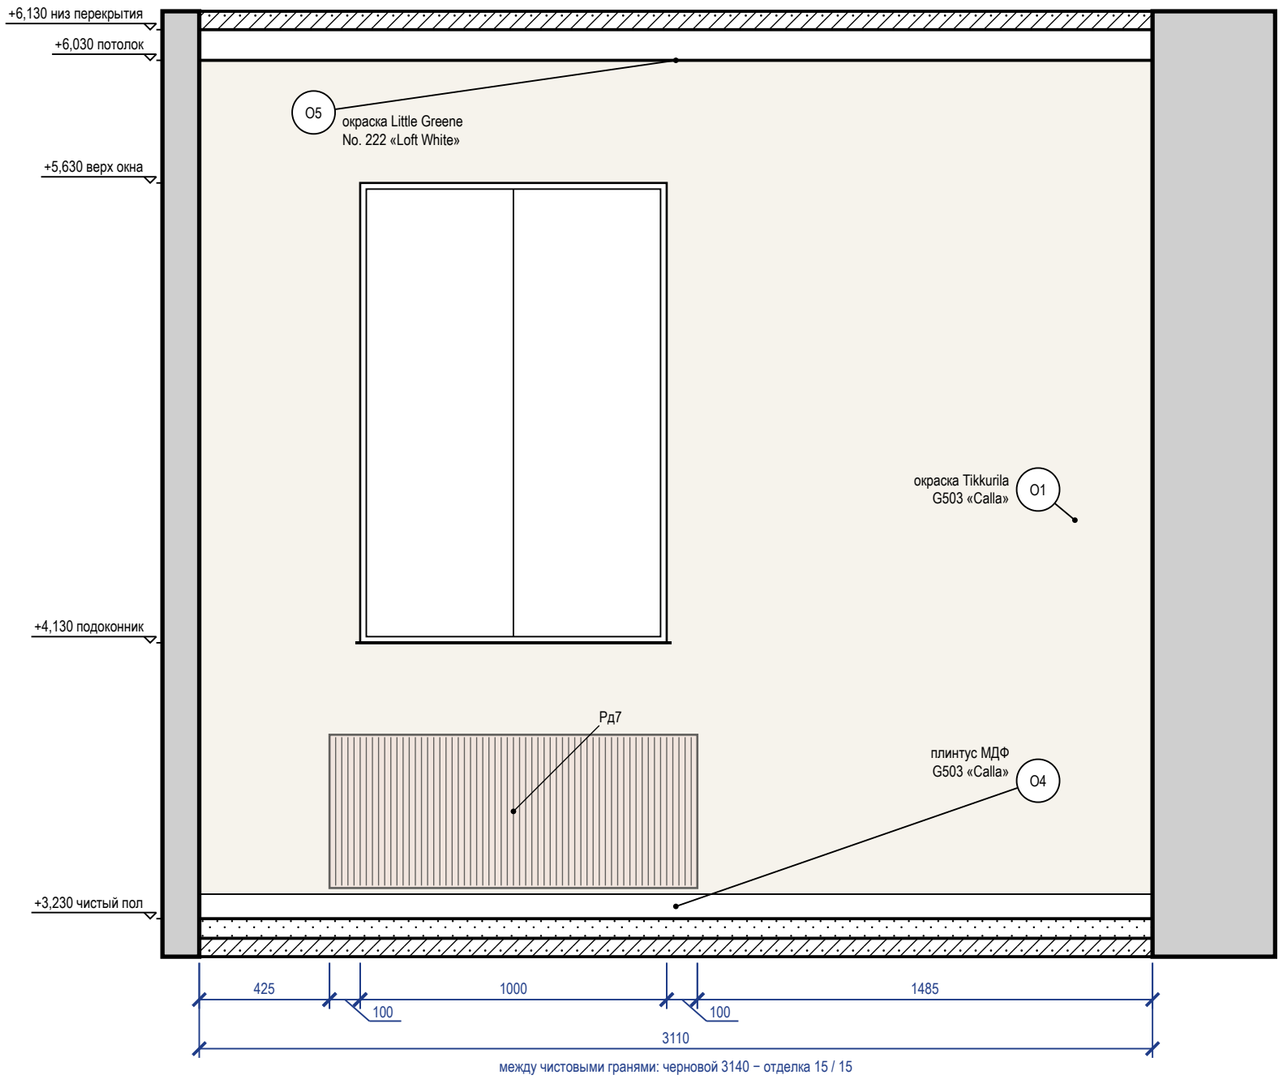


Схема развёрток (М 1:100)

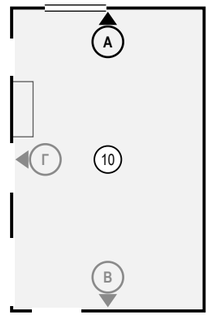

Ведомость отделки (на листе)

Марка	Поверхность	Материал, изделие	Цвет, код	Кол.
О1	стены	окраска, Tikkurila, матовая, подготовка Q3	Tikkurila G503 «Calla»	7,2 м²
О4	плинтус	плинтус МДФ, h 80 мм, аналог: плинтус МДФ под покраску 80×16	Tikkurila G503 «Calla»	3,1 м
О5	потолок	окраска, Little Greene Absolute Matt, глубокоматовая, подготовка Q3	Little Greene No. 222 «Loft White»	15,5 м²

Примечания

1. Размеры — в мм от чистовых поверхностей стен; условные обозначения и общие указания — лист 3.

	Лист	№ док.	Подпись	Дата
Дизайнер	Кырлан А.С.			04.11.26

Проект: Дом 120 м² — **М 1:20**

Развёртка стены А. Холл второго этажа (пом. 10)

Стадия	Лист	Листов
П	104	136

Развёртка стены В


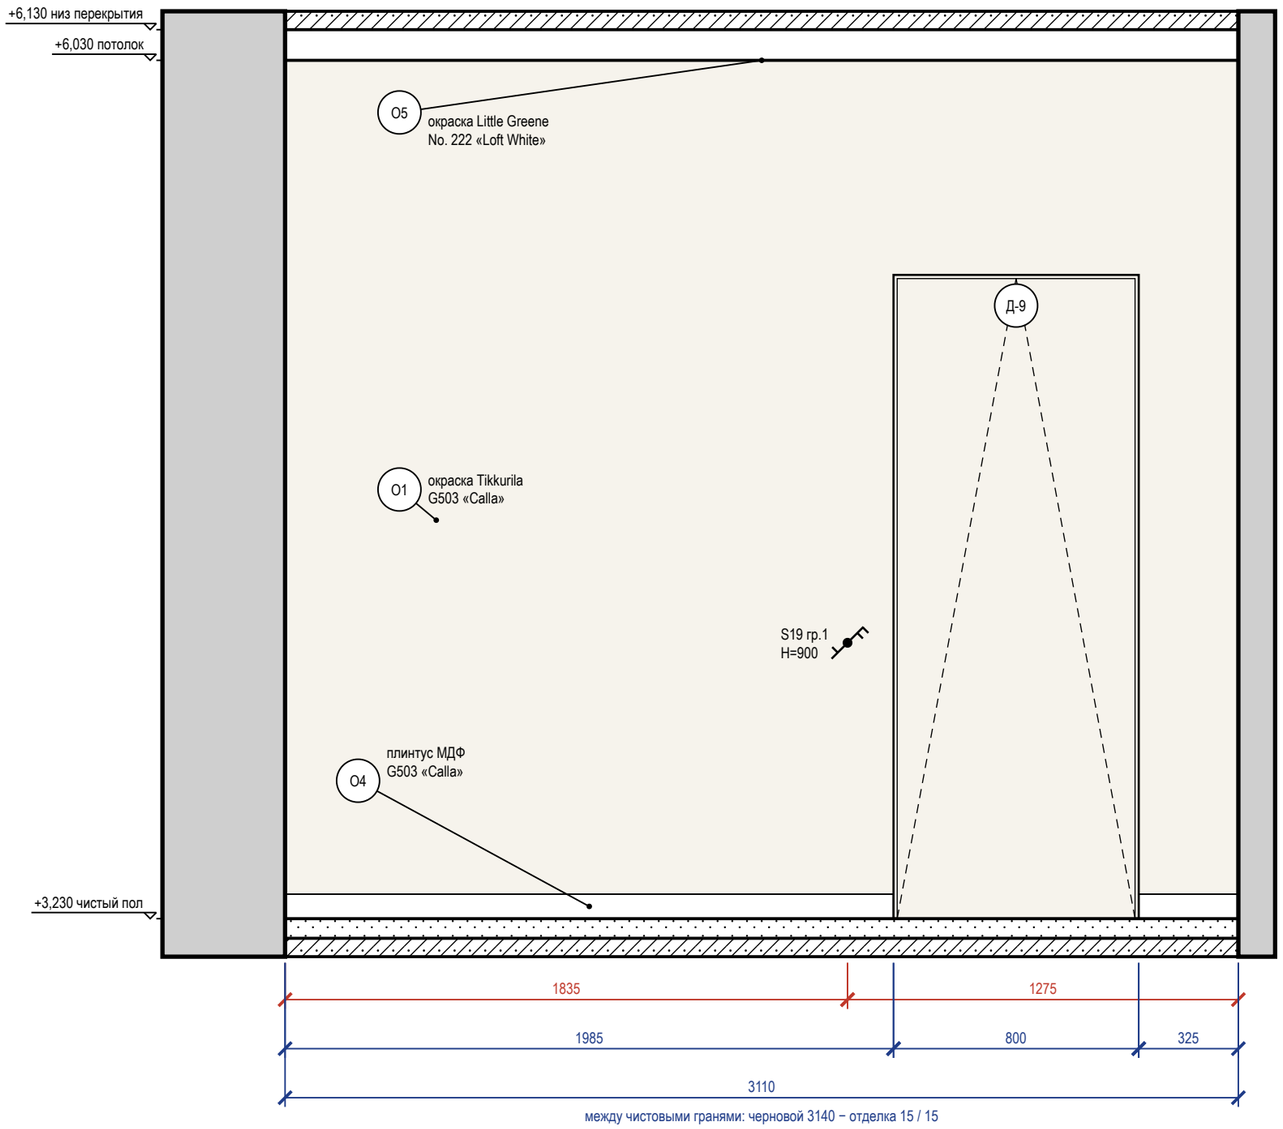


Схема развёрток (М 1:100)

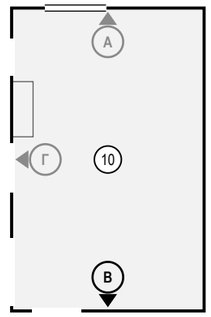

Ведомость отделки (на листе)

Марка	Поверхность	Материал, изделие	Цвет, код	Кол.
О1	стены	окраска, Tikkurila, матовая, подготовка Q3	Tikkurila G503 «Calla»	7 м²
О4	плинтус	плинтус МДФ, h 80 мм, аналог: плинтус МДФ под покраску 80×16	Tikkurila G503 «Calla»	2,3 м
О5	потолок	окраска, Little Greene Absolute Matt, глубокоматовая, подготовка Q3	Little Greene No. 222 «Loft White»	15,5 м²

Примечания

1. Размеры — в мм от чистовых поверхностей стен; условные обозначения и общие указания — лист 3.
2. Двери скрытого монтажа — полотно в плоскости стены, отделка стены по полотну, плинтус прерывается у короба (узел — на листе узлов).

	Лист	№ док.	Подпись	Дата
Дизайнер	Кырлан А.С.			04.11.26

Проект: Дом 120 м² — **М 1:20**

Развёртка стены В. Холл второго этажа (пом. 10)

Стадия	Лист	Листов
П	105	136

Развёртка стены Г


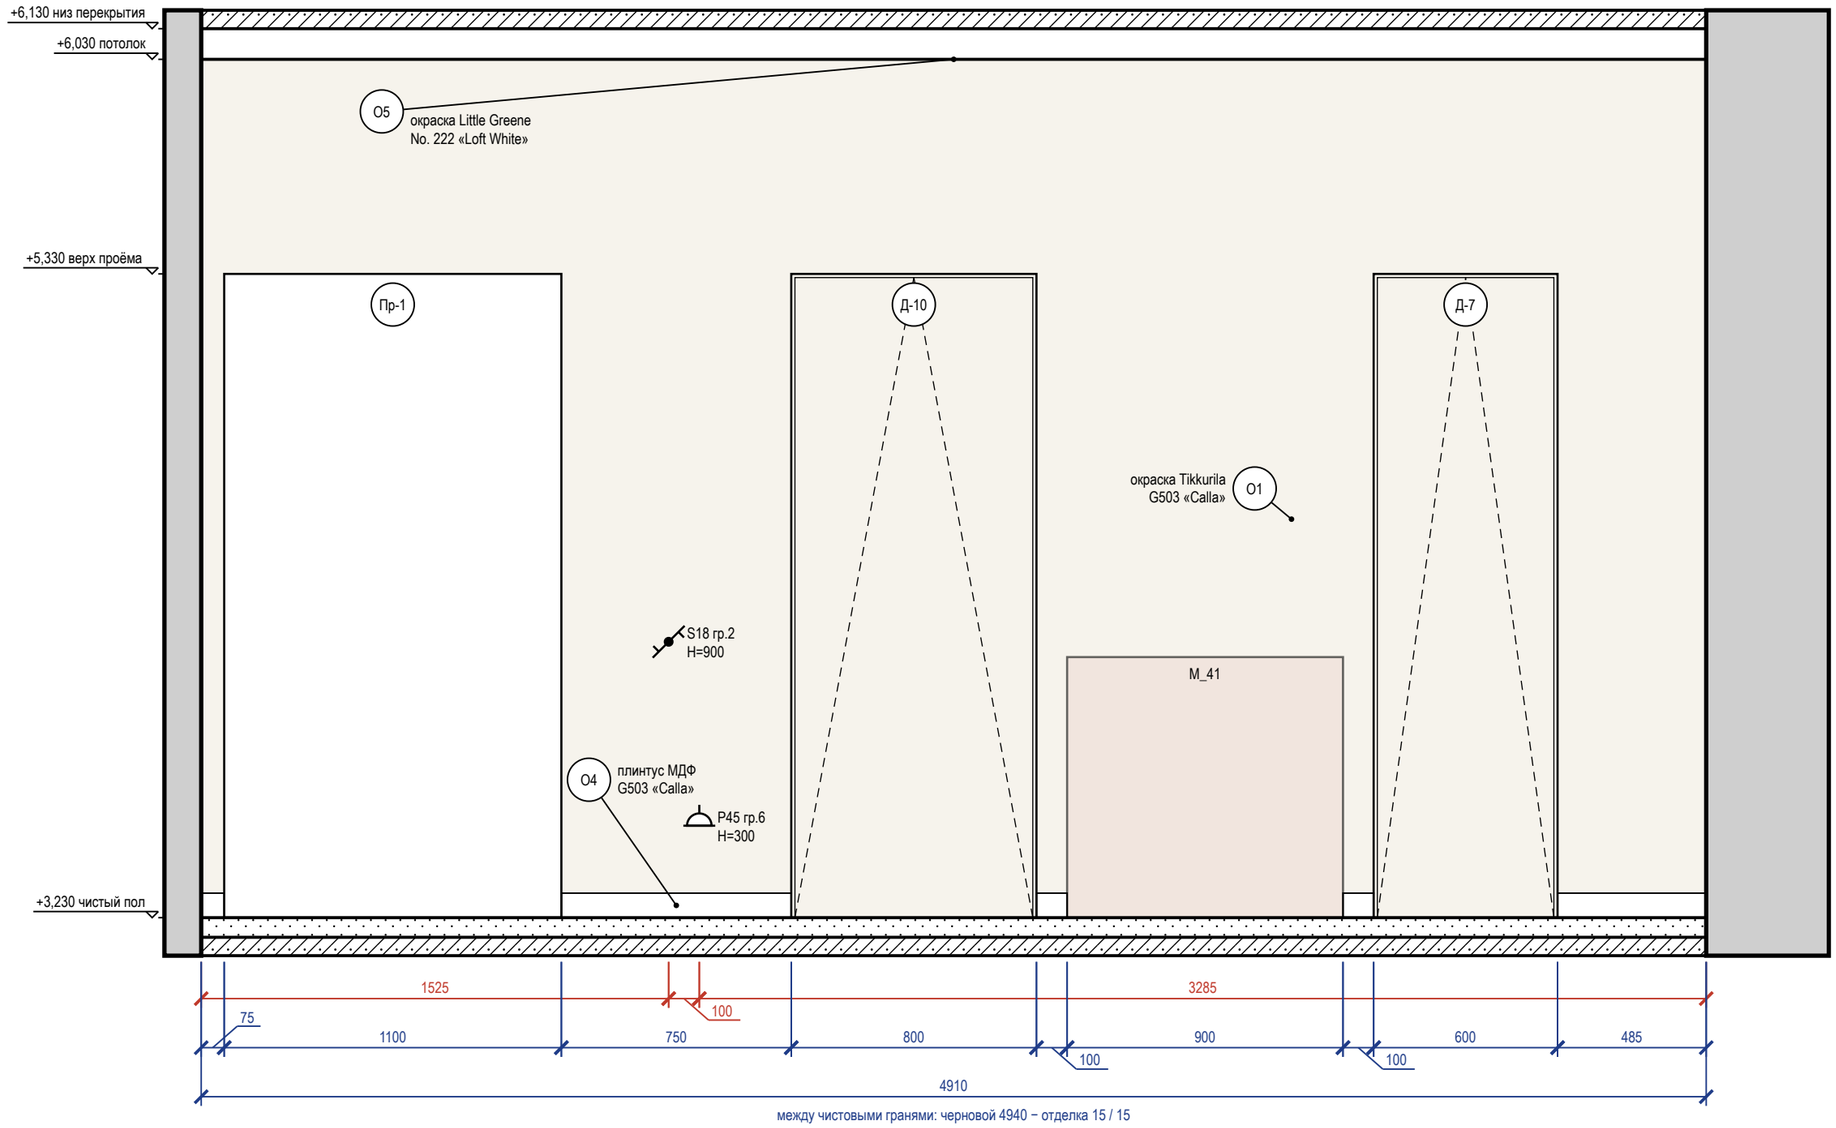


Схема развёрток (М 1:100)

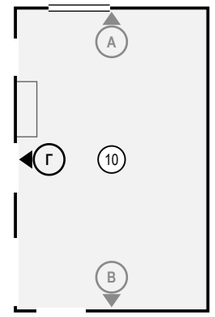

Ведомость отделки (на листе)


Марка	Поверхность	Материал, изделие	Цвет, код	Кол.
О1	стены	окраска, Tikkurila, матовая, подготовка Q3	Tikkurila G503 «Calla»	8,5 м²
О4	плинтус	плинтус МДФ, h 80 мм, аналог: плинтус МДФ под покраску 80×16	Tikkurila G503 «Calla»	1,5 м
О5	потолок	окраска, Little Greene Absolute Matt, глубокоматовая, подготовка Q3	Little Greene No. 222 «Loft White»	15,5 м²

Примечания

1. Размеры — в мм от чистовых поверхностей стен; условные обозначения и общие указания — лист 3.
2. Двери скрытого монтажа — полотно в плоскости стены, отделка стены по полотну, плинтус прерывается у короба (узел — на листе узлов).

					Проект: Дом 120 м²	М 1:20
	Лист	№ док.	Подпись	Дата		
Дизайнер	Кырлан А.С.			04.11.26	Развёртка стены Г. Холл второго этажа (пом. 10)	Стадия: П; Лист: 106; Листов: 136

Развёртка стены А

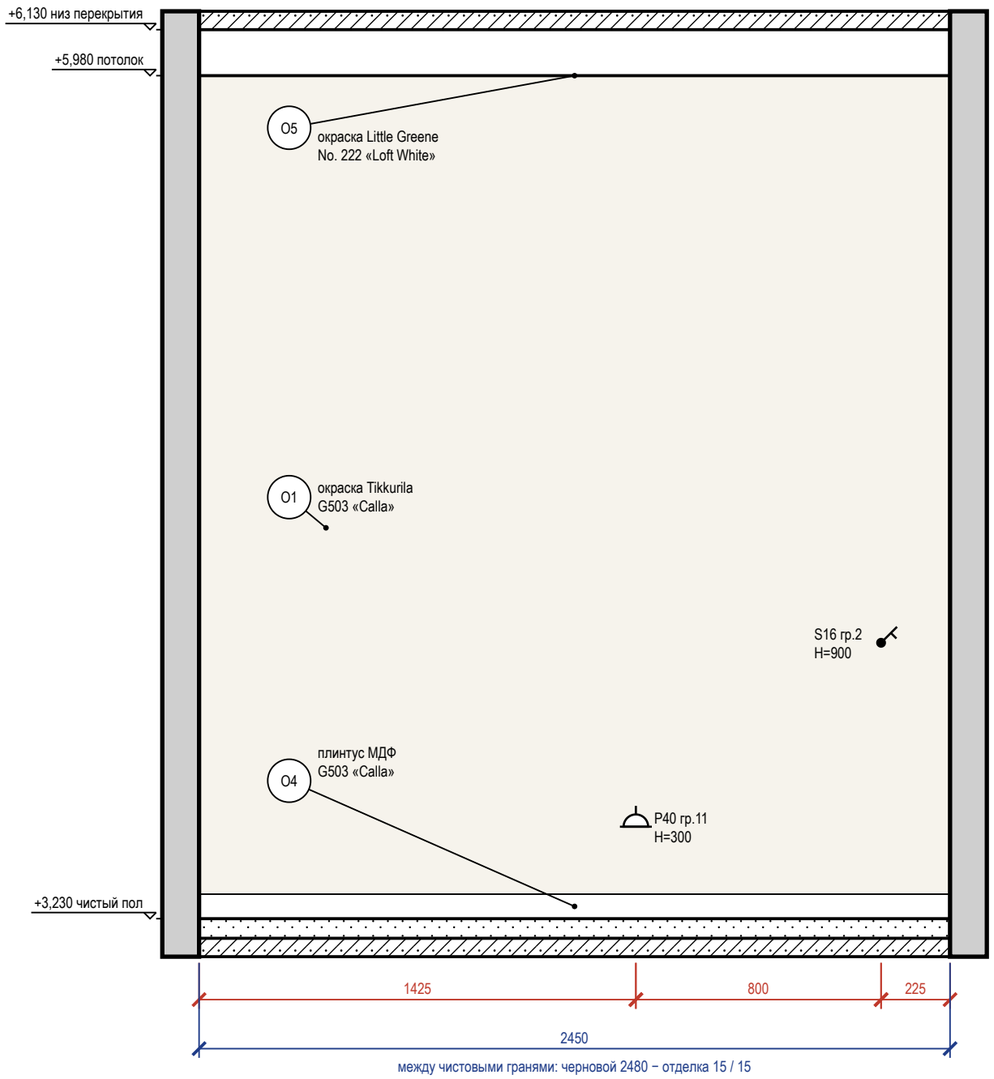

Развёртка стены В


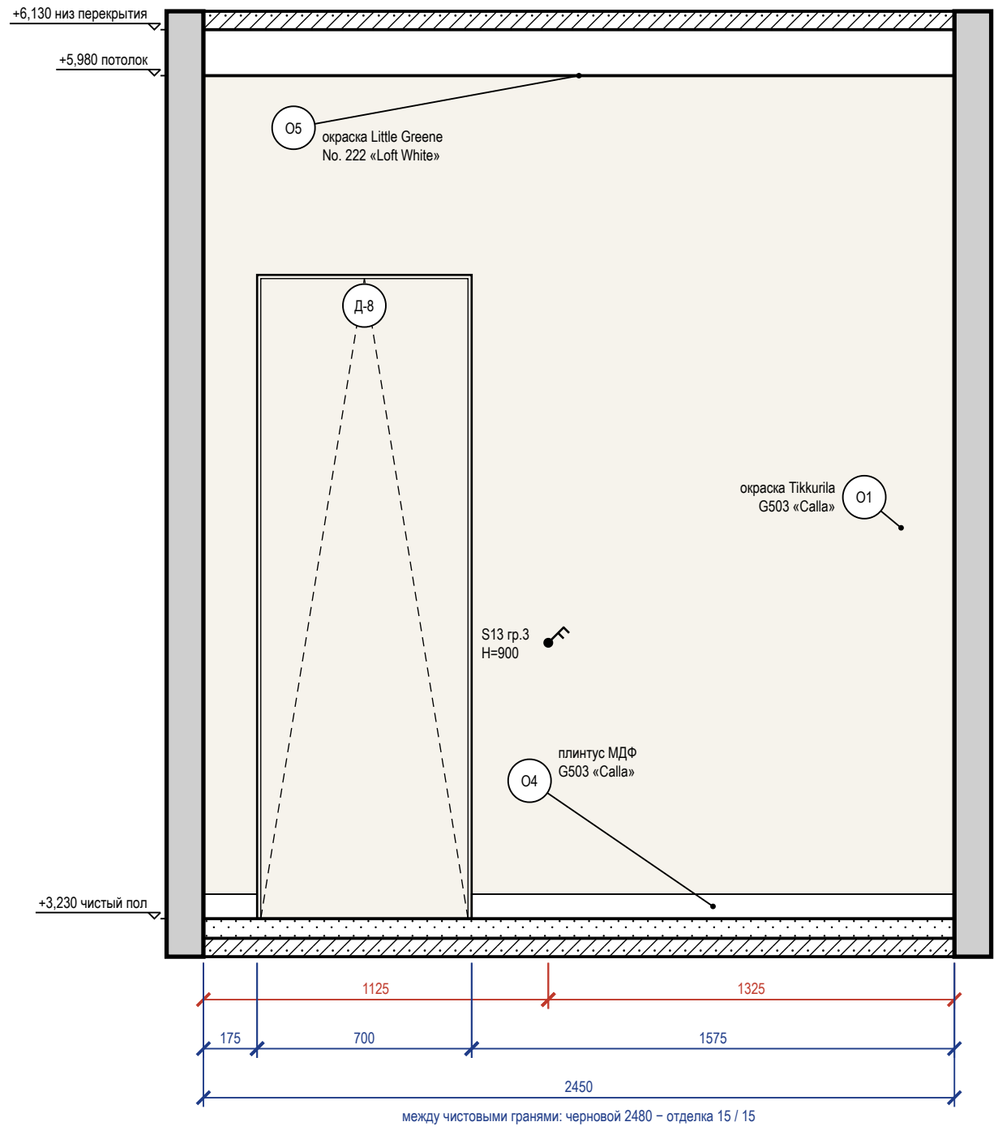


Схема развёрток (М 1:100)

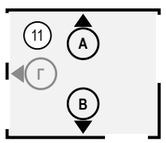

Ведомость отделки (на листе)

Марка	Поверхность	Материал, изделие	Цвет, код	Кол.
О1	стены	окраска, Tikkurila, матовая, подготовка Q3	Tikkurila G503 «Calla»	12 м²
О4	плинтус	плинтус МДФ, h 80 мм, аналог: плинтус МДФ под покраску 80×16	Tikkurila G503 «Calla»	4,2 м
О5	потолок	окраска, Little Greene Absolute Matt, глубокоматовая, подготовка Q3	Little Greene No. 222 «Loft White»	5,2 м²

Примечания

1. Размеры — в мм от чистовых поверхностей стен; условные обозначения и общие указания — лист 3.
2. Двери скрытого монтажа — полотно в плоскости стены, отделка стены по полотну, плинтус прерывается у короба (узел — на листе узлов).

	Лист	№ док.	Подпись	Дата
Дизайнер	Кырлан А.С.			04.11.26

Проект: Дом 120 м² — М 1:20

Развёртки стен А, В. Коридор второго этажа (пом. 11)

Стадия	Лист	Листов
П	107	136

Развёртка стены Г


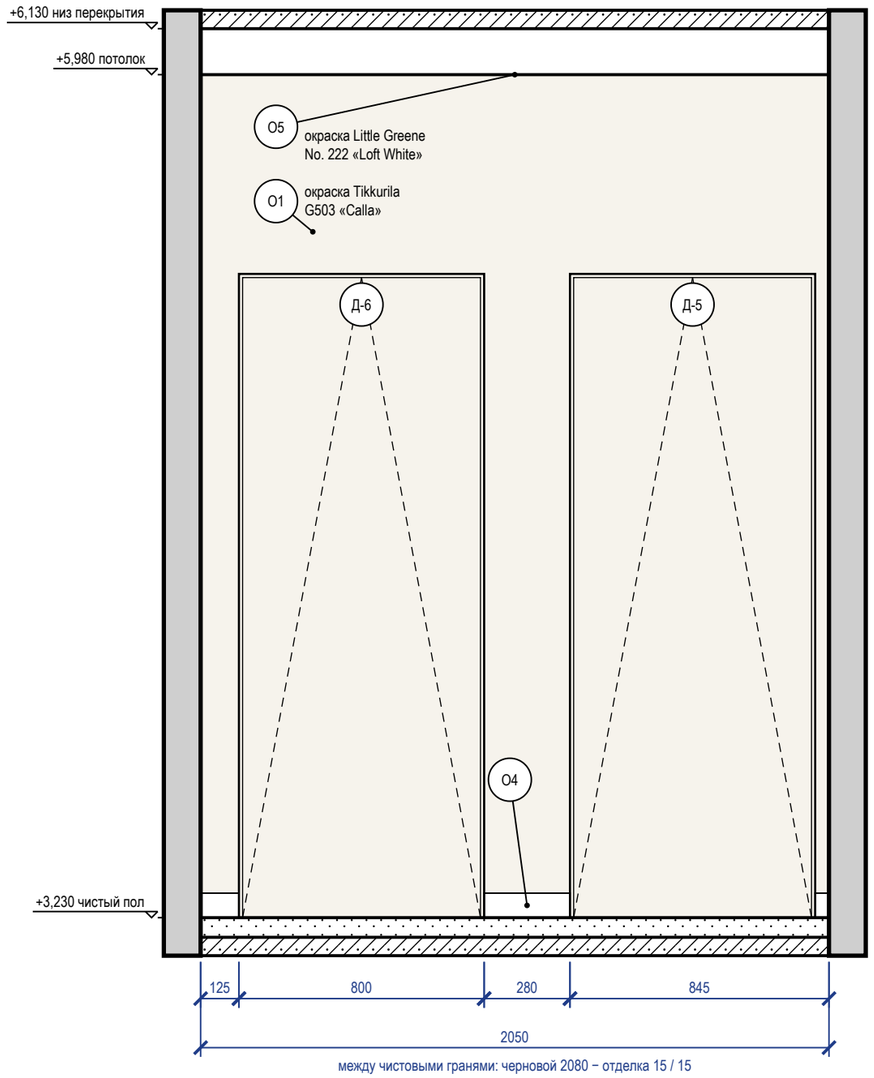


Схема развёрток (М 1:100)

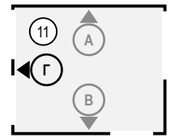

Ведомость отделки (на листе)

Марка	Поверхность	Материал, изделие	Цвет, код	Кол.
О1	стены	окраска, Tikkurila, матовая, подготовка Q3	Tikkurila G503 «Calla»	2,3 м²
О4	плинтус	плинтус МДФ, h 80 мм, аналог: плинтус МДФ под покраску 80×16	Tikkurila G503 «Calla»	0,5 м
О5	потолок	окраска, Little Greene Absolute Matt, глубокоматовая, подготовка Q3	Little Greene No. 222 «Loft White»	5,2 м²

Примечания

1. Размеры — в мм от чистовых поверхностей стен; условные обозначения и общие указания — лист 3.
2. Двери скрытого монтажа — полотно в плоскости стены, отделка стены по полотну, плинтус прерывается у короба (узел — на листе узлов).

					Проект: Дом 120 м²	М 1:20
	Лист	№ док.	Подпись	Дата		
Дизайнер	Кырлан А.С.			04.11.26	Развёртка стены Г. Коридор второго этажа (пом. 11)	
					Стадия: П	Лист: 108 / Листов: 136

Развёртка стены А


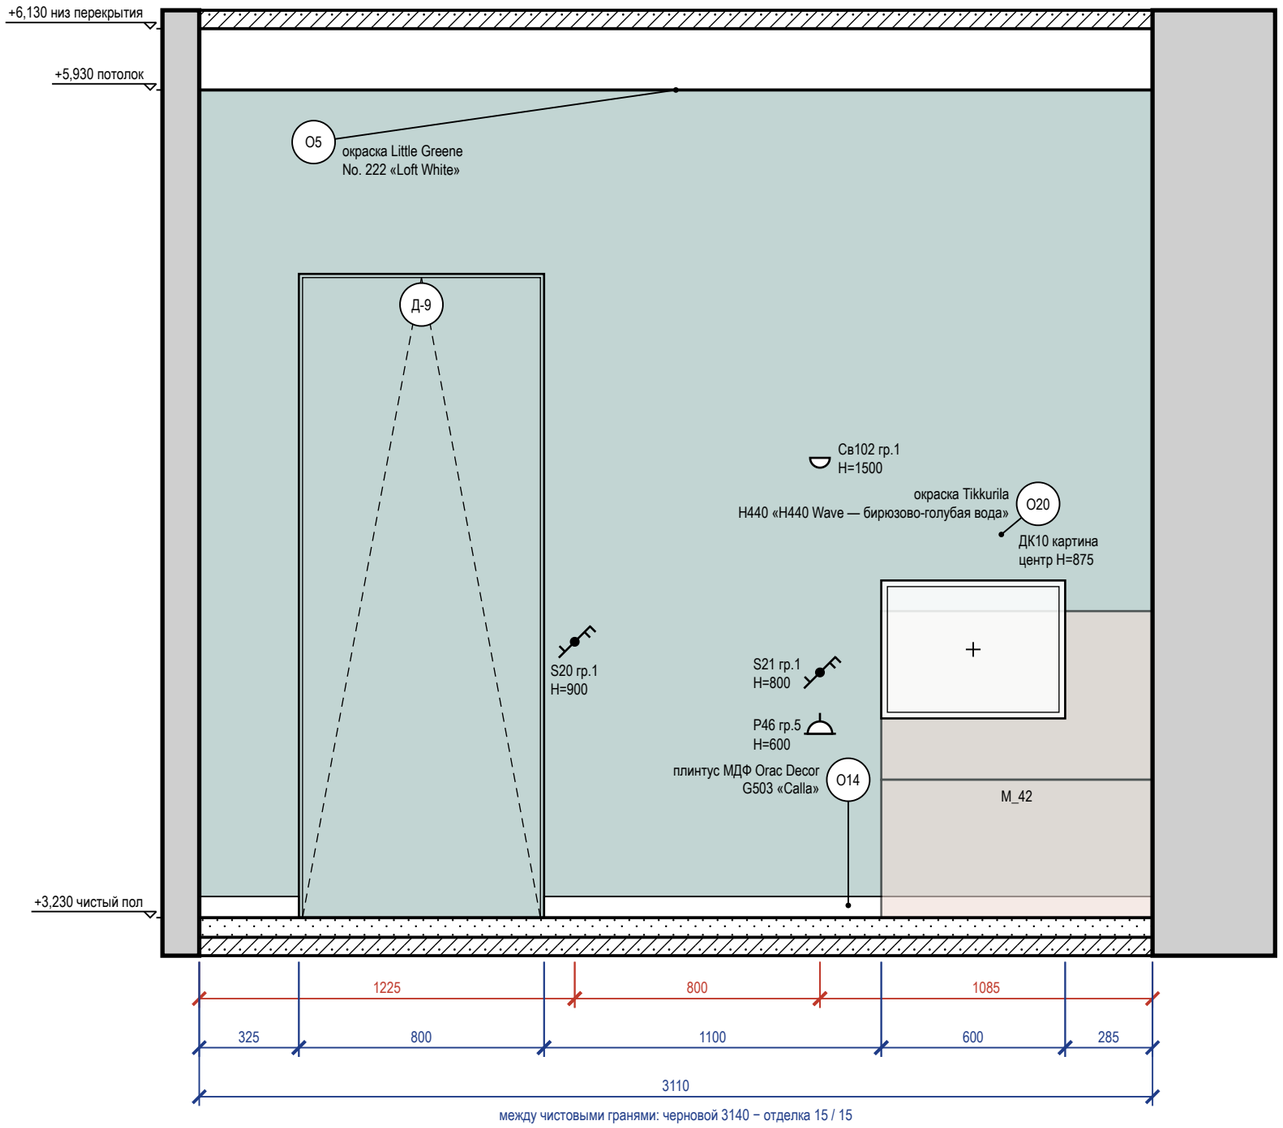


Схема развёрток (М 1:100)

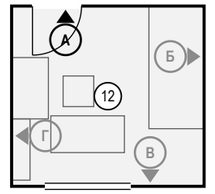

Ведомость отделки (на листе)

Марка	Поверхность	Материал, изделие	Цвет, код	Кол.
О5	потолок	окраска, Little Greene Absolute Matt, глубокоматовая, подготовка Q3	Little Greene No. 222 «Loft White»	9,2 м²
О14	плинтус	плинтус МДФ, Orac Decor Contour (Luxxus), h 69 мм, SX165	Tikkurila G503 «Calla»	2,3 м
О20	акцентная стена	окраска, Tikkurila, шелковисто-матовая, подготовка Q3	Tikkurila H440 «H440 Wave бирюзово-голубая вода»	6,7 м²

Примечания

1. Размеры — в мм от чистовых поверхностей стен; условные обозначения и общие указания — лист 3.
2. Картины и зеркала крепить к основанию по паспорту изделия (закладные и анкеры — в перечне скрытых работ); крест — ось центра предмета.
3. Двери скрытого монтажа — полотно в плоскости стены, отделка стены по полотну, плинтус прерывается у короба (узел — на листе узлов).
4. Потолок — у каждой стены свой, по плану потолков (ПТ8); ступени — зоной, кромка короба перед нишей — тонкой линией; в поле потолка: ПТ7 +6,030.

					Проект: Дом 120 м²	М 1:20
	Лист	№ док.	Подпись	Дата		
Дизайнер	Кырлан А.С.			04.11.26	Развёртка стены А. Детская вторая (пом. 12)	
					Стадия: П	Лист: 109 / Листов: 136

Развёртка стены Б


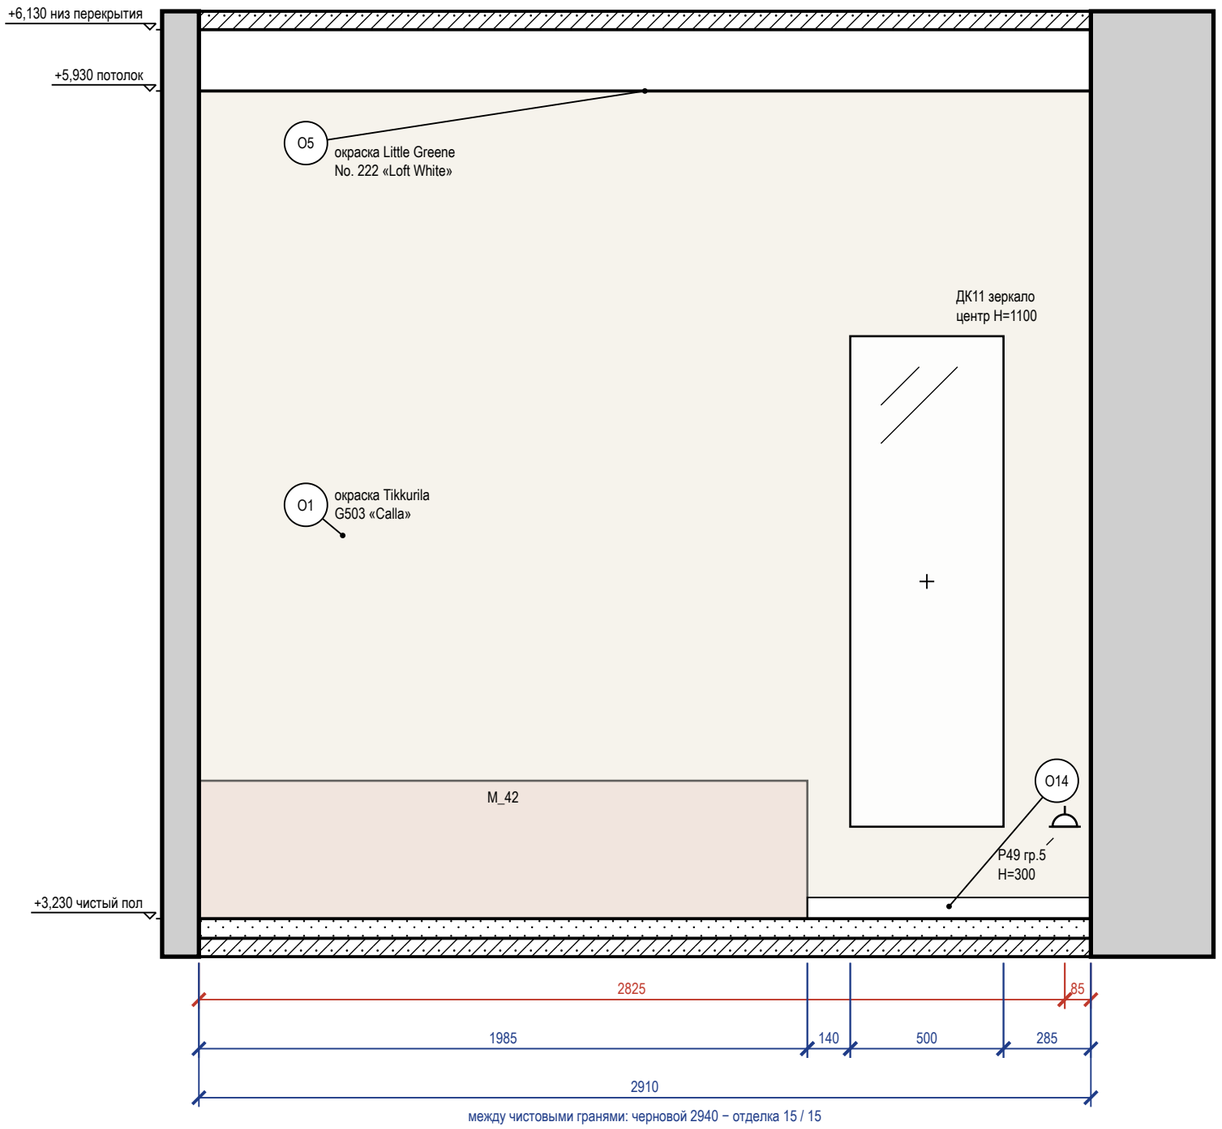


Схема развёрток (М 1:100)

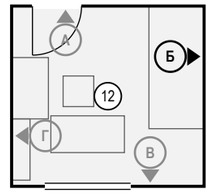

Ведомость отделки (на листе)

Марка	Поверхность	Материал, изделие	Цвет, код	Кол.
О1	стены	окраска, Tikkurila, шелковисто-матовая, подготовка Q3	Tikkurila G503 «Calla»	7,9 м²
О5	потолок	окраска, Little Greene Absolute Matt, глубокоматовая, подготовка Q3	Little Greene No. 222 «Loft White»	9,2 м²
О14	плинтус	плинтус МДФ, Orac Decor Contour (Luxxus), h 69 мм, SX165	Tikkurila G503 «Calla»	0,9 м

Примечания

1. Размеры — в мм от чистовых поверхностей стен; условные обозначения и общие указания — лист 3.
2. Картины и зеркала крепить к основанию по паспорту изделия (закладные и анкеры — в перечне скрытых работ); крест — ось центра предмета.
3. Потолок — у каждой стены свой, по плану потолков (ПТ8); ступени — зоной, кромка короба перед нишей — тонкой линией; в поле потолка: ПТ7 +6,030.

					Проект: Дом 120 м²	М 1:20
	Лист	№ док.	Подпись	Дата		
Дизайнер	Кырлан А.С.			04.11.26	Развёртка стены Б. Детская вторая (пом. 12)	Стадия: П; Лист: 110; Листов: 136

Развёртка стены В


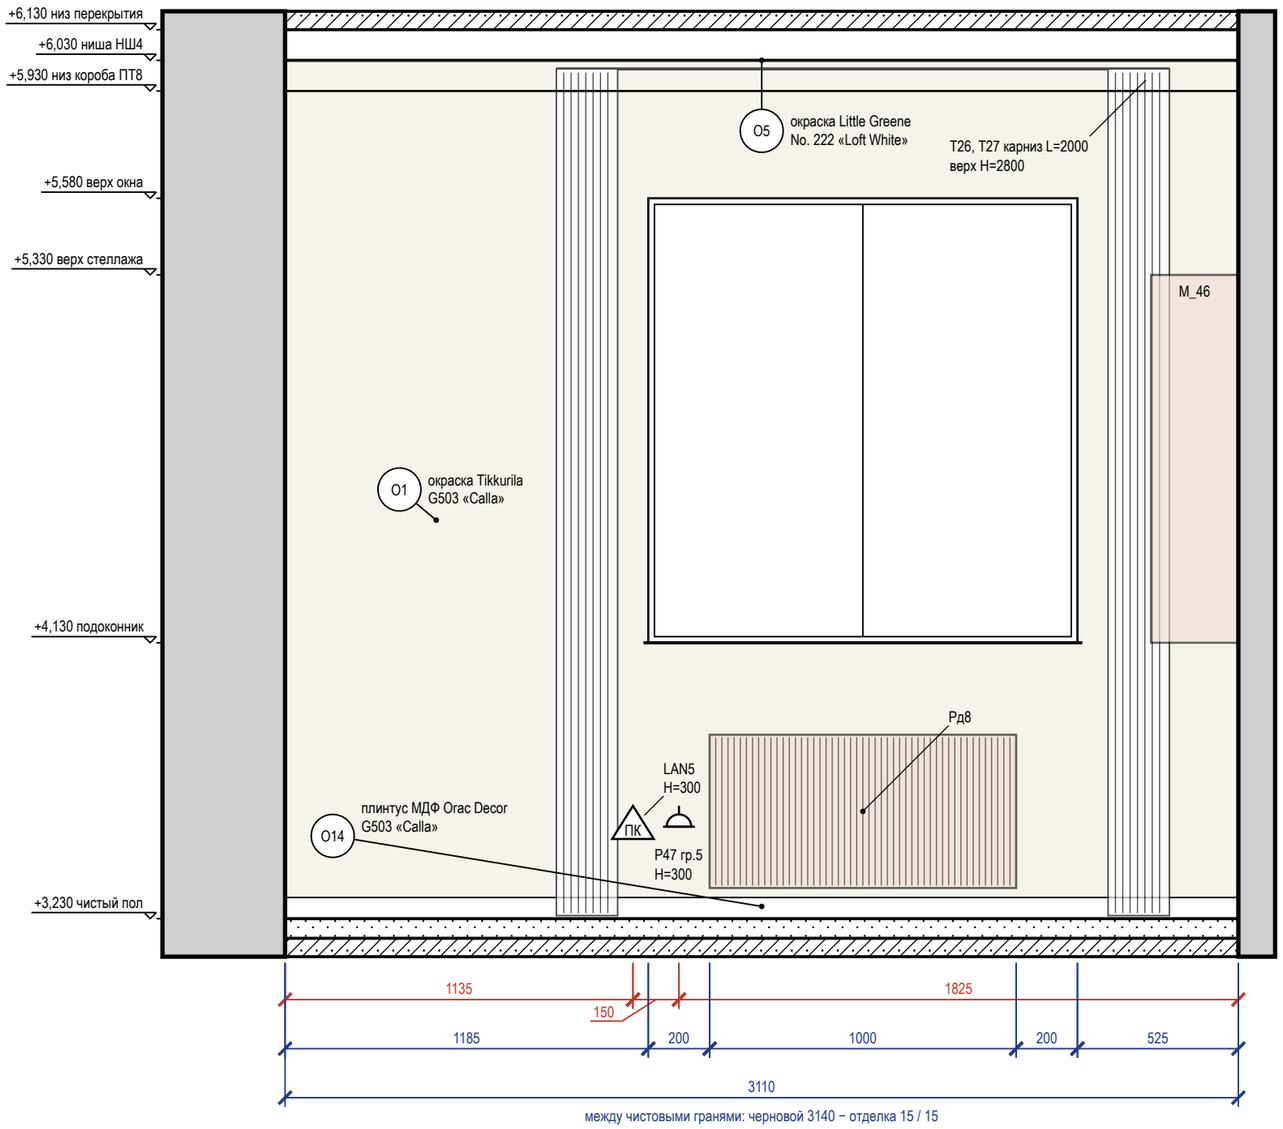


Схема развёрток (М 1:100)

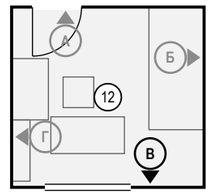

Ведомость отделки (на листе)

Марка	Поверхность	Материал, изделие	Цвет, код	Кол.
О1	стены	окраска, Tikkurila, шелковисто-матовая, подготовка Q3	Tikkurila G503 «Calla»	6,7 м²
О5	потолок	окраска, Little Greene Absolute Matt, глубокоматовая, подготовка Q3	Little Greene No. 222 «Loft White»	9,2 м²
О14	плинтус	плинтус МДФ, Orac Decor Contour (Luxxus), h 69 мм, SX165	Tikkurila G503 «Calla»	3,1 м

Примечания

1. Размеры — в мм от чистовых поверхностей стен; условные обозначения и общие указания — лист 3.
2. Карнизы (шины) — по ведомости текстиля декоратора: длина L и верх H на развёртке — те же числа, что в ведомости; крепление — до окраски потолка.
3. Потолок — у каждой стены свой, по плану потолков (НШ4, ПТ8); ступени — зоной, кромка короба перед нишей — тонкой линией; в поле потолка: ПТ7 +6,030.

					Проект: Дом 120 м²	М 1:20
	Лист	№ док.	Подпись	Дата		
Дизайнер	Кырлан А.С.			04.11.26	Развёртка стены В. Детская вторая (пом. 12)	

Стадия	Лист	Листов
П	111	136

Развёртка стены Г


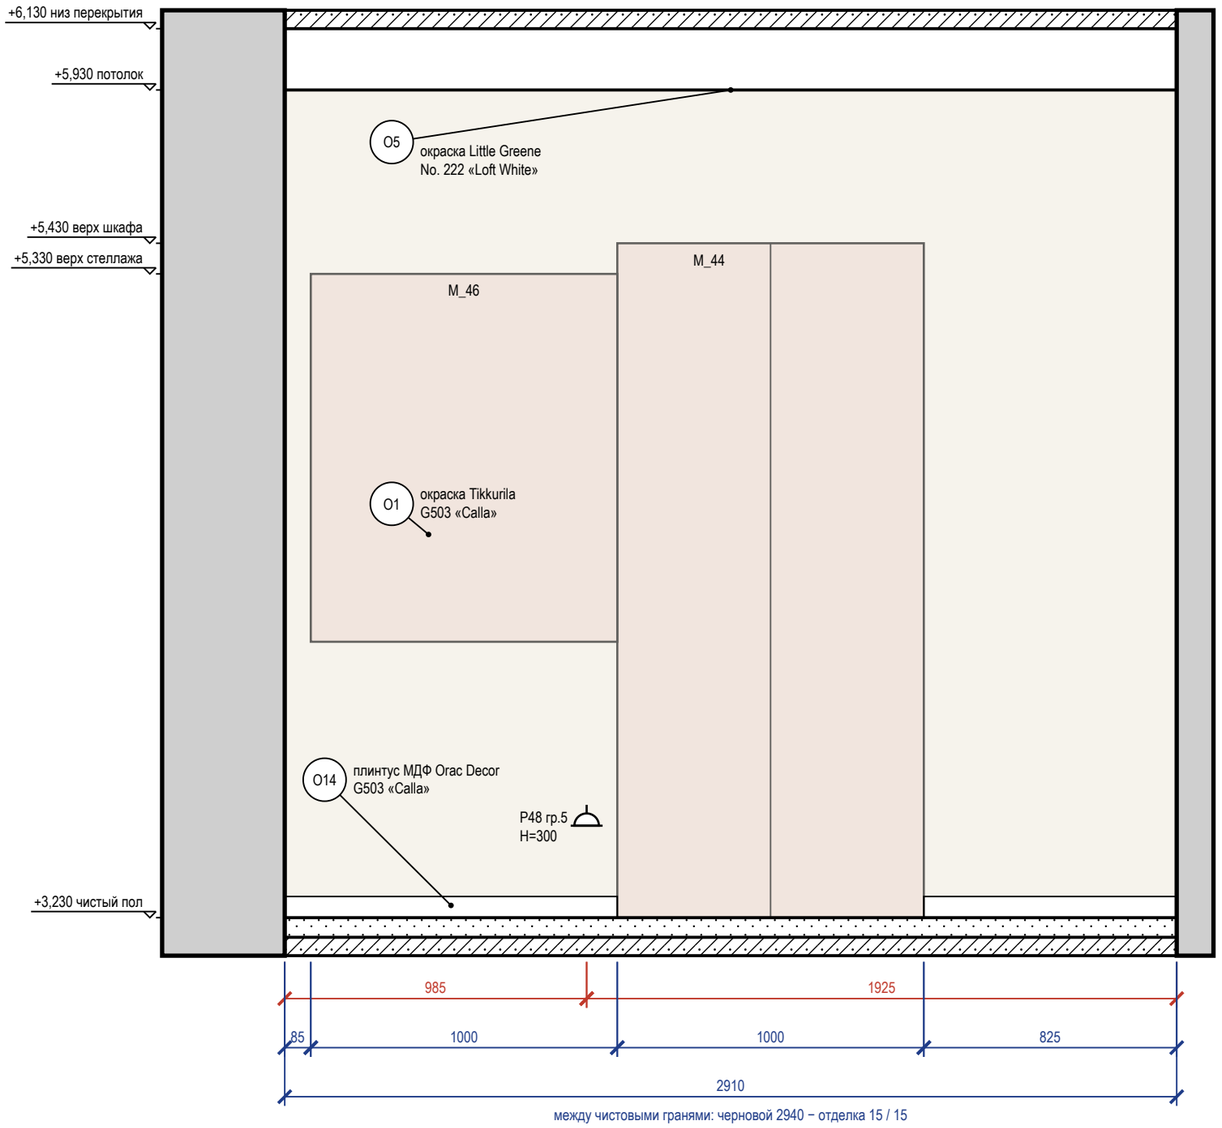


Схема развёрток (М 1:100)

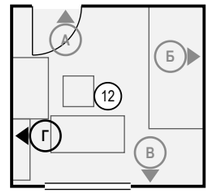

Ведомость отделки (на листе)

Марка	Поверхность	Материал, изделие	Цвет, код	Кол.
O1	стены	окраска, Tikkurila, шелковисто-матовая, подготовка Q3	Tikkurila G503 «Calla»	7,9 м²
O5	потолок	окраска, Little Greene Absolute Matt, глубокоматовая, подготовка Q3	Little Greene No. 222 «Loft White»	9,2 м²
O14	плинтус	плинтус МДФ, Orac Decor Contour (Luxxus), h 69 мм, SX165	Tikkurila G503 «Calla»	1,9 м


Примечания

1. Размеры — в мм от чистовых поверхностей стен; условные обозначения и общие указания — лист 3.
2. Потолок — у каждой стены свой, по плану потолков (ПТ8); ступени — зоной, кромка короба перед нишей — тонкой линией; в поле потолка: ПТ7 +6,030.

					Проект: Дом 120 м² — М 1:20
	Лист	№ док.	Подпись	Дата	Развёртка стены Г. Детская вторая (пом. 12)
Дизайнер	Кырлан А.С.			04.11.26	

Стадия	Лист	Листов
П	112	136

Развёртка стены А

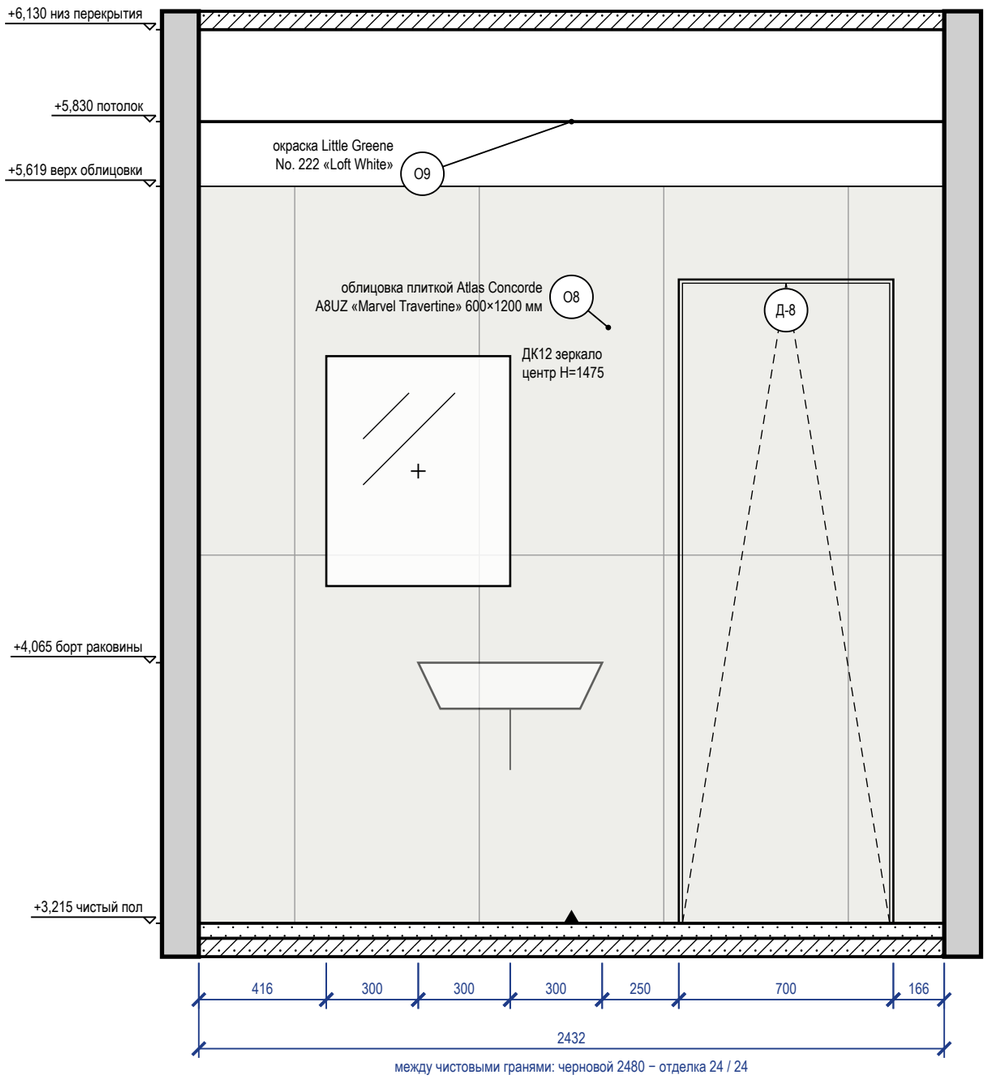

Развёртка стены Б


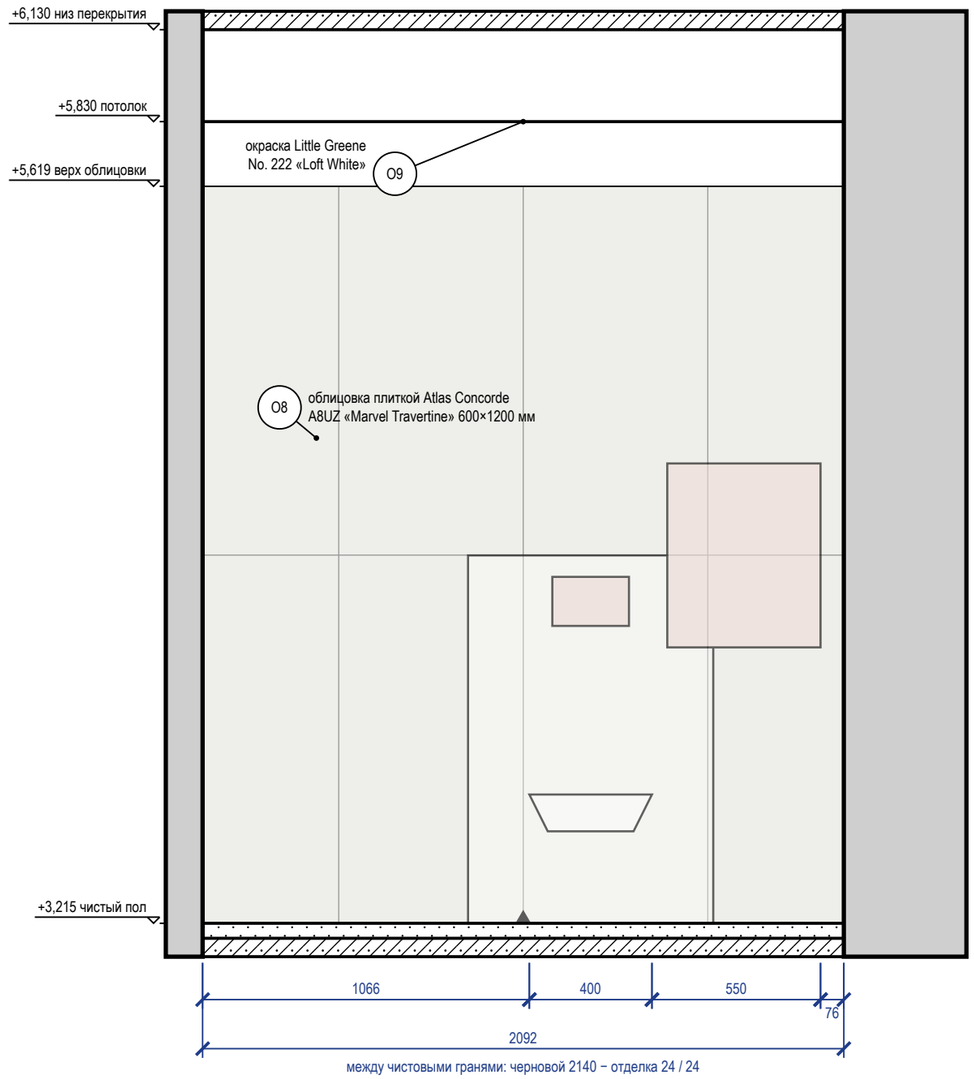


Схема развёрток (М 1:100)

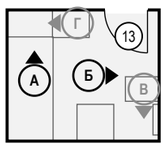

Ведомость отделки (на листе)

Марка	Поверхность	Материал, изделие	Цвет, код	Кол.
О8	стены	облицовка плиткой, Atlas Concorde Marvel Travertine, 600×1200×9 мм, A8UZ, затирка CG2WA	Atlas Concorde A8UZ «Marvel Travertine»	9,4 м²
О9	потолок	окраска, Little Greene Intelligent Bathroom, матовая, подготовка Q3	Little Greene No. 222 «Loft White»	5,3 м²


Примечания

1. Размеры — в мм от чистовых поверхностей стен; условные обозначения и общие указания — лист 3.
2. Стены А, Б показаны двумя видами: здесь — архитектурная развёртка (мебель, отделка, проёмы, высоты), электроточки и выводы ВК с привязками и таблицей — на листе 114 («Привязки»).
3. Схема мебели, приборов и декора не является технической документацией для производства мебели; габариты — по паспортам изделий.
4. Облицовка — по сетке швов 2 мм, раскладка от оси стены (треугольник у пола), целые ряды от пола; подрезки — по листу раскладки плитки.
5. Гидроизоляция в 2 слоя, заход на стены 200 мм; над ванной — до 2000 и 300 мм за борт — до облицовки, с актом скрытых работ и тестом проливом (узел — на листе узлов).
6. Картины и зеркала крепить к основанию по паспорту изделия (закладные и анкеры — в перечне скрытых работ); крест — ось центра предмета.
7. Двери скрытого монтажа — полотно в плоскости стены, отделка стены по полотну, плинтус прерывается у короба (узел — на листе узлов).

					Проект: Дом 120 м² — М 1:20
	Лист	№ док.	Подпись	Дата	Развёртки стен А, Б. Санузел второго этажа (пом. 13)
Дизайнер	Кырлан А.С.			04.11.26	

Стадия	Лист	Листов
П	113	136

Развёртка стены А: электроточки и выводы

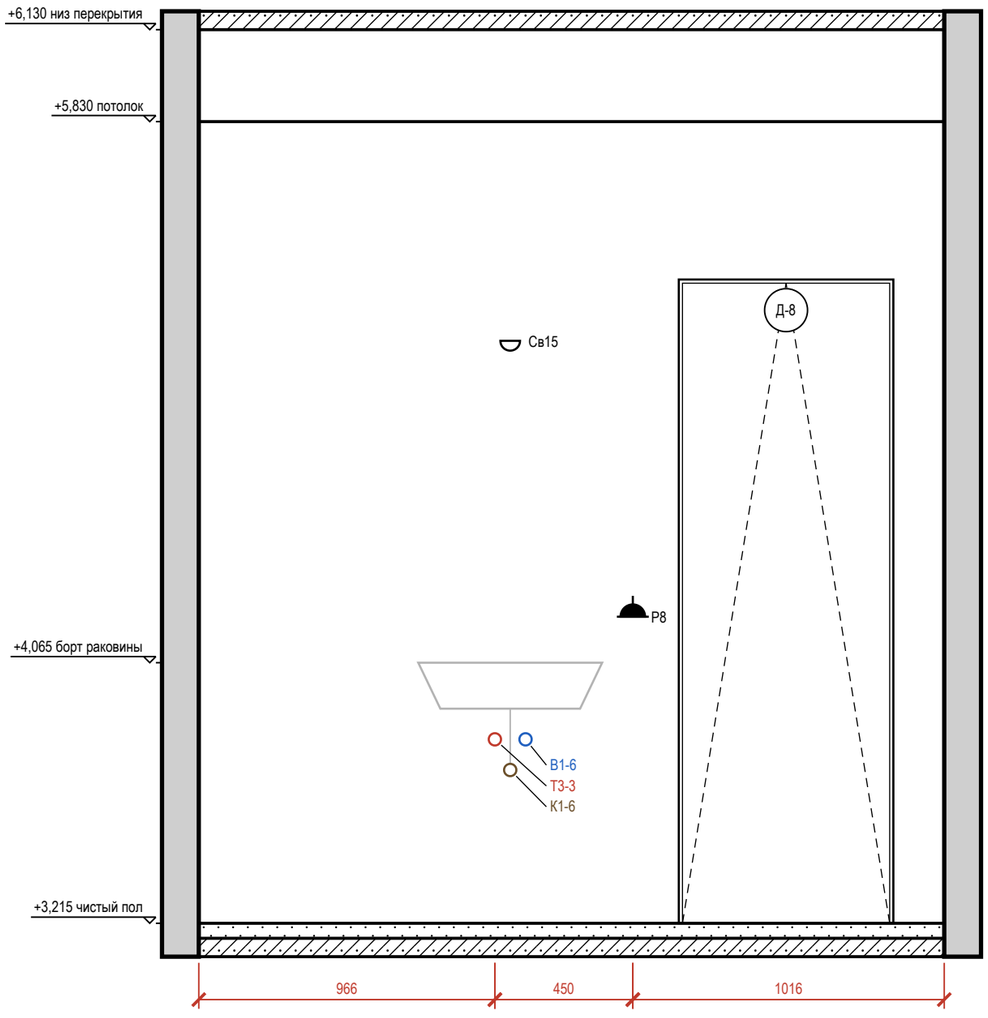

Развёртка стены Б: электроточки и выводы

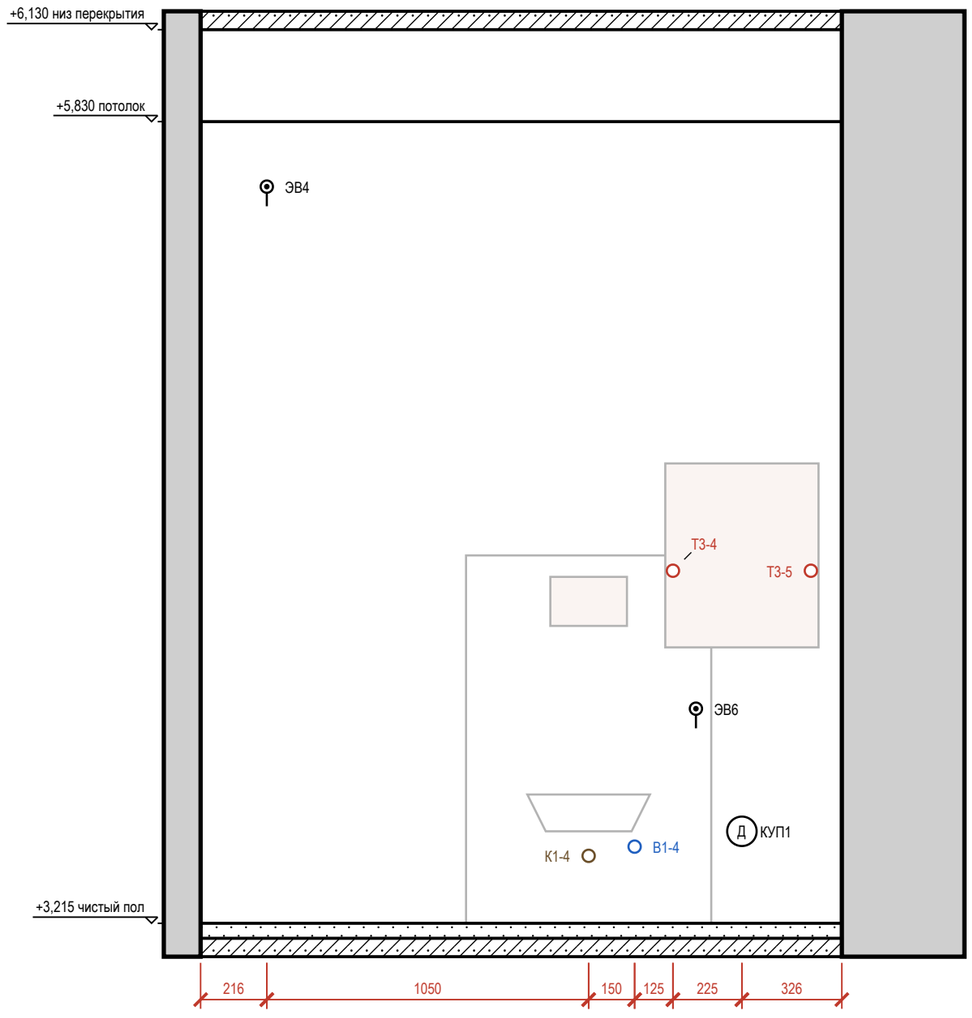


Таблица привязок электроточек и выводов

Стена	Марка	Назначение	От угла, мм	Н от пола, мм	Примечание
А	Т3-3	горячая вода — умывальник	966	600	межос. 100
А	К1-6	канализация — умывальник	1016	500	Ø50
А	Св15	светильник настенный	1016	1900	гр. 3
А	В1-6	холодная вода — умывальник	1066	600	межос. 100
А	Р8	розетка: фен у умывальника	1416	1000	гр. 16, IP44
Б	ЭВ4	вывод кабеля: вентилятор ВР1 (таймер выбега)	216	2403	гр. 3

Стена	Марка	Назначение	От угла, мм	Н от пола, мм	Примечание
Б	К1-4	канализация — унитаз подвесной	1266	220	Ø110
Б	В1-4	холодная вода — унитаз подвесной	1416	250	в раме инсталляции
Б	Т3-4	горячая вода — полотенцесушитель	1541	1150	подача, межос. 450; байпас и краны
Б	ЭВ6	вывод кабеля: полотенцесушитель П10	1616	700	гр. 16
Б	КУП1	КУП — уравнивание потенциалов (ДСУП)	1766	300	
Б	Т3-5	горячая вода — полотенцесушитель	1991	1150	обратка

Условные обозначения

- розетка влагозащищённая IP44
- вывод кабеля для подключения прибора (без розетки), марка ЭВ
- светильник настенный (бра), Н — высота оси
- вывод В1 (код — в ведомости привязок)
- вывод Т3 (код — в ведомости привязок)
- вывод К1 (код — в ведомости привязок)
- привязки точек и выводов от угла и от пола, мм

Примечания


1. Вид «Привязки» стен А, Б — электроточки и выводы ВК; архитектурная развёртка (мебель, отделка, проёмы, высоты) — на листе 113. Мебель и приборы — подложкой для ориентира; их марки и обозначения мебели, проёмов и стен — там же.
2. Привязки — в мм: по горизонтали от левого чистового угла стены до оси изделия, Н — от чистого пола до оси; все точки — в таблице привязок. Красная цепочка — привязки по осям; точки ближе 120 мм одна к другой в цепочку не дробятся — их привязки только в таблице.
3. У знака — марка электроточки (Р — розетка, S — выключатель, Св — светильник, ЭВ — вывод кабеля); условные обозначения и общие указания — лист 3.
4. Коды выводов ВК: В1 — холодная вода, Т3 — горячая вода, К1 — канализация; номер после дефиса — номер вывода на листе выводов сантехники.

					Проект: Дом 120 м² — М 1:20
	Лист	№ док.	Подпись	Дата	Привязки электроточек и выводов ВК, стены А, Б. Санузел второго этажа (пом. 13)
Дизайнер	Кырлан А.С.			04.11.26	

Стадия	Лист	Листов
П	114	136


выпуск 04.11.2026 № 406ed8a6ce · стр. 114 из 136

Развёртка стены В

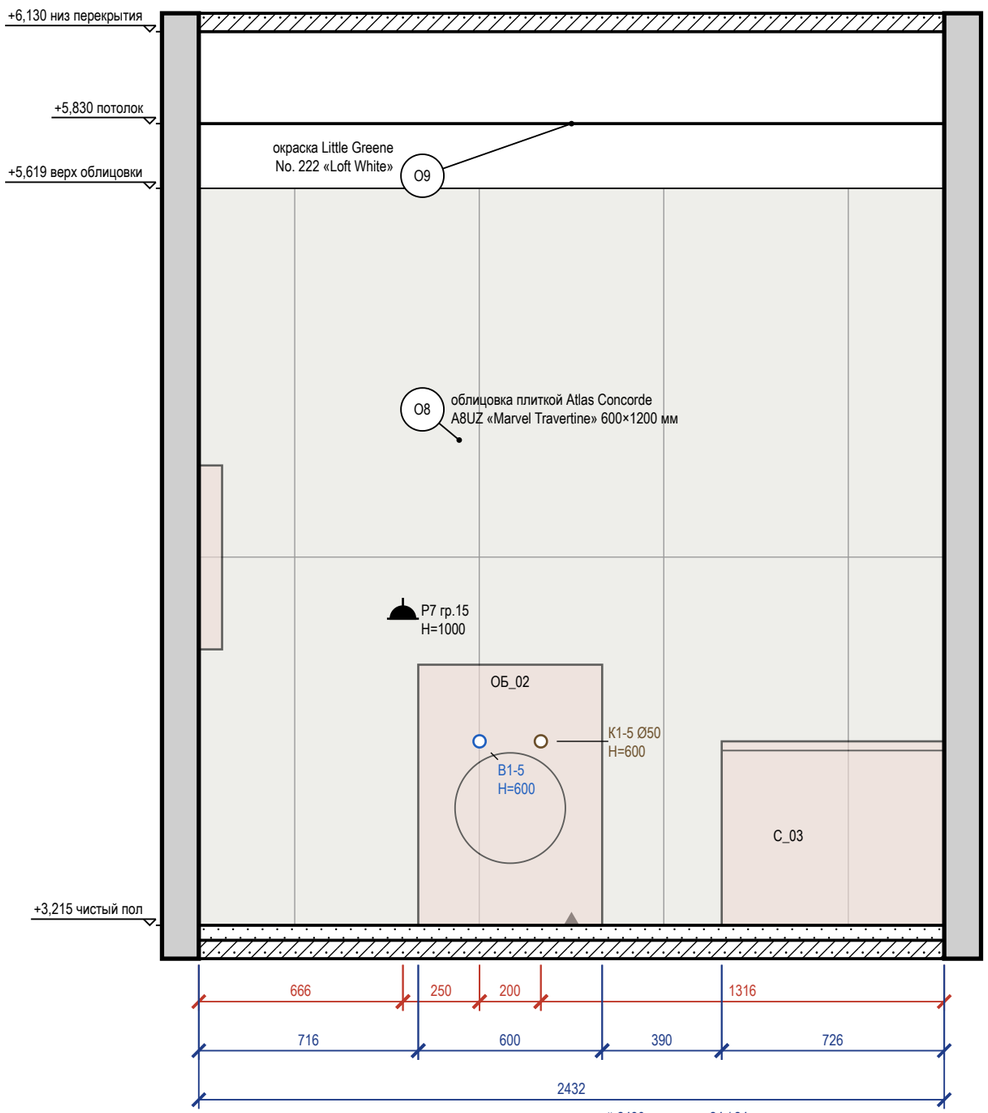


между чистовыми гранями: черновой 2480 − отделка 24 / 24

Развёртка стены Г

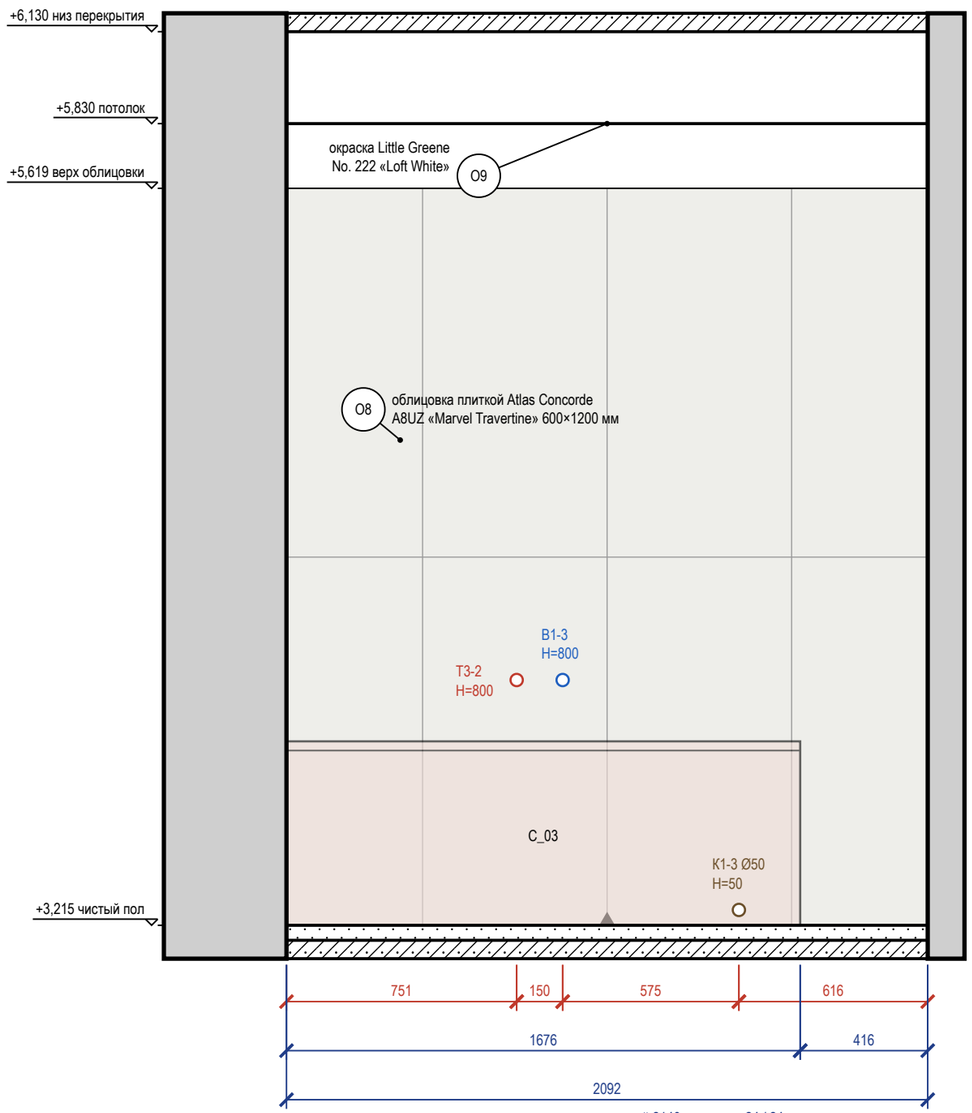

между чистовыми гранями: черновой 2140 − отделка 24 / 24

Схема развёрток (М 1:100)

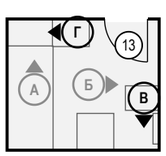

Ведомость отделки (на листе)

Марка	Поверхность	Материал, изделие	Цвет, код	Кол.
О8	стены	облицовка плиткой, Atlas Concorde Marvel Travertine, 600×1200×9 мм, A8UZ, затирка CG2WA	Atlas Concorde A8UZ «Marvel Travertine»	10,9 м²
О9	потолок	окраска, Little Greene Intelligent Bathroom, матовая, подготовка Q3	Little Greene No. 222 «Loft White»	5,3 м²

Примечания

1. Размеры — в мм от чистовых поверхностей стен; условные обозначения и общие указания — лист 3.
2. Схема мебели, приборов и декора не является технической документацией для производства мебели; габариты — по паспортам изделий.
3. Выводы ВК — коды и высоты по листу выводов сантехники.
4. Облицовка — по сетке швов 2 мм, раскладка от оси стены (треугольник у пола), целые ряды от пола; подрезки — по листу раскладки плитки.
5. Гидроизоляция в 2 слоя, заход на стены 200 мм; над ванной — до 2000 и 300 мм за борт — до облицовки, с актом скрытых работ и тестом проливом (узел — на листе узлов).

					Проект: Дом 120 м²	М 1:20
	Лист	№ док.	Подпись	Дата		
Дизайнер	Кырлан А.С.			04.11.26	Развёртки стен В, Г. Санузел второго этажа (пом. 13)	Стадия: П; Лист: 115; Листов: 136

Комплект предварительный по пунктам этих таблиц. Пока по пункту нет ответа или решения, показанное на указанном листе — допущение проектировщика, а не утверждённое решение.
Сводка: открытых вопросов — 9 (из них ждут факта объекта — 3: контрольного обмера, обследования или документа); изменений в реестре — 2, из них без подписи — 2.

Открытые вопросы и принятые допущения

№	Формулировка	Вид	Кто решает	Если решения нет	Лист, где это проявляется
К-1	Бриф задаёт 11 помещений с габаритами и этажами, но не их взаимное расположение, контур дома и толщины стен: раскладка этажей, контур 9600 × 8000 и перегородки подобраны проектировщиком под габариты брифа. До заказа мебели, дверей и материалов нужен обмер или проект дома (АР).	Отсутствует Ждёт: обмера	Архитектор-планировщик	размеры на листах — предложение проектировщика по брифу, уточняются по месту; мебель на заказ и материалы по ним не заказывать	л. 6, 7 — План планировки от заказчика л. 6–9, 14–17, 19, 20, 26–29, 35, 36, 39–41, 43, 44, 52–57, 59–66, 104–108, 113–115 — 1-й этаж л. 19, 20 — План размещения мебели и оборудования
К-2	Высота потолка 2900 мм — по брифу (не замерена); конструкция и толщина перекрытия не заданы — принято 330 мм с полом, отметка чистого пола 2-го этажа +3,230. Нужен проект КР дома.	Отсутствует	Архитектор-планировщик	высоты на развёртках, отметка 2-го этажа и лестница — от принятых 2900 / +3,230, уточнить по проекту КР	л. 6, 7 — План планировки от заказчика л. 6–9, 14–17, 19, 20, 26–29, 35, 36, 39–41, 43, 44, 52–57, 59–66, 104–108, 113–115 — 1-й этаж л. 43, 44 — План потолков
К-3	Лестница по брифу — из холла 1-го этажа; место, тип (одномаршевая прямая, 17 подъёмов 190 × 250, марш 1000), конструкция и ограждение — предложение проектировщика. Расчёт несущей конструкции марша и проёма в перекрытии — проект КР.	Отсутствует	Архитектор-планировщик	лестница на планах — предложение, к изготовлению не выдаётся до проекта КР	л. 6, 7 — План планировки от заказчика л. 6–9, 14–17, 19, 20, 26–29, 35, 36, 39–41, 43, 44, 52–57, 59–66, 104–108, 113–115 — 1-й этаж
К-4	Разрешённая мощность дома по ТУ неизвестна, принята 15 кВт.	Отсутствует	Инженер-электрик	щит и группы рассчитаны на 15 кВт; при других ТУ пересчёт	л. 50 — Однолинейная схема щита л. 52, 53 — План розеток и электровыводов л. 6–9, 14–17, 19, 20, 26–29, 35, 36, 39–41, 43, 44, 52–57, 59–66, 104–108, 113–115 — 1-й этаж
К-5	Тип дома, материал и конструкция стен и перекрытия, несущие стены, положение стояков, выпусков канализации и вентканалов в брифе не заданы; проект дома (АР, КР, ВК, ОВ) не передан. Стояки и вентканалы на планах показаны по предложению проектировщика.	Отсутствует Ждёт: документа	Архитектор-планировщик	все существующие стены считаются несущими: проёмы и перегородки — предложение, к строительству не выдаются; стояки — предложение	л. 6, 7 — План планировки от заказчика л. 6–9, 14–17, 19, 20, 26–29, 35, 36, 39–41, 43, 44, 52–57, 59–66, 104–108, 113–115 — 1-й этаж л. 28, 29 — Схема разводки водопровода и канализации
К-6	Источник отопления и горячей воды (котёл: газ / электро, его место, котельная) брифом не задан; в составе помещений брифа котельной нет. Отопительные приборы на листах — водяные радиаторы под окнами при любом источнике тепла.	Решение	Инженер ОВ	радиаторы и трассы — предложение; котёл, котельная и ввод газа — после ответа заказчика	л. 63, 64 — План отопления л. 6–9, 14–17, 19, 20, 26–29, 35, 36, 39–41, 43, 44, 52–57, 59–66, 104–108, 113–115 — 1-й этаж л. 28, 29 — Схема разводки водопровода и канализации
К-7	Климатический подрайон (СП 131.13330) не задан: принят не северный — жилые комнаты и кухня под потолком от 2,5 м (СП 54, п. 5.12); в IA, IБ, IГ, IД, IVA — от 2,7 м.	Отсутствует Ждёт: документа	Архитектор-планировщик	отметки потолков жилых — по 2,5 м; при северном подрайоне уровни ниже 2,7 м пересчитать до заказа каркаса	л. 43, 44 — План потолков л. 6–9, 14–17, 19, 20, 26–29, 35, 36, 39–41, 43, 44, 52–57, 59–66, 104–108, 113–115 — 1-й этаж
К-8	Кухня (пом. 1): мойка M_02 и модули M_01, M_03 стоят под окном 1500 × 1500 стены А с низом проёма +0,900 — подоконник в уровне столешницы (+0,900). Смеситель мойки упирается в створку, открывающуюся внутрь, примыкание столешницы к откосу и подоконнику не решено. Нужно решение заказчика: створка над мойкой глухая или поворотно-откидная (откидывание над смесителем), либо поднять низ окна (подоконник выше столешницы на высоту смесителя), либо столешница заходит в проём вместо подоконника.	Решение Ждёт: решения	Дизайнер интерьера	столешница у окна не раскраивается, мойка M_02 и смеситель не заказываются; монтажная схема кухни показывает проём и конфликт	л. 10 — Кухня (пом. 1). Монтажная схема
К-9	Умывальник C_05 (пом. 13 «Санузел второго этажа»), выпуск К1-4 Ø50: трасса до Ст К1-1 (2,54 м) идёт под дверным проёмом Д-8 — короб над полом там не поставить. Решить: (а) прибор ближе к стояку Ст К1-1 (без прохода под проёмом); (б) выпуск в полу с подъёмом пола помещения на 130 мм; (в) насосная установка (КНС) у прибора — по паспорту, требует согласования. Решение меняет санузел (высоты, раскладку плитки) — за автором с заказчиком.	Спорно Ждёт: решения	Инженер ВК (вода, канализация)	выпуск К1-4 и прибор C_05 не выполнять до решения; остальное — по листам	л. 28, 29 — Схема разводки водопровода и канализации л. 6–9, 14–17, 19, 20, 26–29, 35, 36, 39–41, 43, 44, 52–57, 59–66, 104–108, 113–115 — 1-й этаж л. 26, 27 — План выводов сантехники

					Проект: Дом 120 м²
	Лист	№ док.	Подпись	Дата	Открытые вопросы, принятые допущения и конфликты. Лист 1 из 2
Дизайнер	Кырлан А.С.			04.11.26	

Стадия	Лист	Листов
П	116	136

Изменения проекта после выпуска листов (реестр изменений)


№	Дата	Лист	Было	Стало	Кто решил, подпись
ИЗ-1	30.10.2026	л. 26, 27 — План выводов сантехники л. 6–9, 14–17, 19, 20, 26–29, 35, 36, 39–41, 43, 44, 52–57, 59–66, 104–108, 113–115 — 1-й этаж л. 28, 29 — Схема разводки водопровода и канализации л. 19, 20 — План размещения мебели и оборудования л. 40, 41 — План размещения дверей л. 52, 53 — План розеток и электровыводов л. 39 — Раскладка плитки. Санузел второго этажа. Развёртки стен	Санузел второго этажа (пом. 13, 2600×2200): раковина С_05 (стена А 500…1100) и стиральная машина ОБ_02 (стена Г 300…900) пересекались в углу, перед люком машины стояла раковина; ванна С_03 (стена В 150…1850) заходила в проход перед Д-8 на 500 из 800 мм; унитаз С_04 (стена Б 900…1300) накрывал стояки Ст К1-1 / В1-1; полотенцесушитель С_06 в 2,3 м от стояка ГВС; при открытом полотне Д-8 в помещение не пройти.	Ванна С_03 — вдоль стены Г (offset 500, x 3800…4550, y 6300…8000); умывальник С_05 — стена А offset 800…1400; стиральная машина ОБ_02 — стена В offset 1200…1800 (перед люком 1150 мм); унитаз С_04 — стена Б offset 1150…1550 (250 мм до стояков — короб с люком); полотенцесушитель С_06 — стена Б 1600…2100; Д-8 — петли у правого откоса. Точки ЭОМ санузла перенесены за приборами (Р7 — стена В, Р8 — offset 1500, Св15 — 1100, КУП1 и В6 — стена Б). Трасса выпуска умывальника под проёмом Д-8 остаётся — К-9. Знак «**» у приборов до подписи автора.	Не утверждено: подписи нет. решение исполнителя; предложение проектировщика, на утверждение А. С. Кырлана
ИЗ-2	30.10.2026	л. 19, 20 — План размещения мебели и оборудования л. 6–9, 14–17, 19, 20, 26–29, 35, 36, 39–41, 43, 44, 52–57, 59–66, 104–108, 113–115 — 1-й этаж л. 76 — Развёртка стены А. Холл с лестницей (пом. 2) л. 81 — Развёртка стены В. Кабинет (пом. 3) л. 98 — Развёртка стены В. Детская (пом. 7) л. 104 — Развёртка стены А. Холл второго этажа (пом. 10) л. 111 — Развёртка стены В. Детская вторая (пом. 12) л. 52, 53 — План розеток и электровыводов	Мебель закрывала радиаторы: банкетка М_19 (холл) на Рд3, стол М_20 (кабинет) на Рд4, стол М_33 (детская) на Рд6, стеллаж М_41 (холл 2-го этажа) перед Рд7, стол М_43 (детская вторая) на Рд8; на пяти развёртках служебная фраза «прибор в корпусе не решён». Розетка Р16 прихожей за радиатором Рд2. Назначения Р9/Р10 «у кровати» и Р11 «у комода» в кабинете, Р42/Р47 «у комода» в детских — по образцу, не по мебели. Группы щита 15–17 без точек на планах.	М_19 и М_41 — у стены Г холлов (offset 1200); столы М_20, М_33, М_43 — 300 мм от лицевой плоскости радиатора (x,y), стулья за ними; радиаторы открыты. Р16 — стена В offset 2300; Р34 offset 2600. Назначения точек переписаны по расстановке. Р7 (стиральная машина) — группа 15, Р8, Р33, В6 (фены, полотенцесушитель) — группа 16, Р17 (ЩС) — группа 17. Знак «**» у переставленной мебели до подписи автора.	Не утверждено: подписи нет. решение исполнителя; предложение проектировщика, на утверждение А. С. Кырлана

Примечания


1. Номера листов — по ведомости рабочих чертежей комплекта (лист «Общие данные»).
2. Графа «Если решения нет» показывает состояние решения на листах; влияние на сроки и стоимость по пунктам не оценивалось.
3. Пункт, по которому принято решение, при следующем выпуске комплекта из таблиц исключается.

					Проект: Дом 120 м²			
	Лист	№ док.	Подпись	Дата	Открытые вопросы, принятые допущения и конфликты. Лист 2 из 2	Стадия	Лист	Листов
Дизайнер	Кырлан А.С.			04.11.26		П	117	136


Вид с фасадами

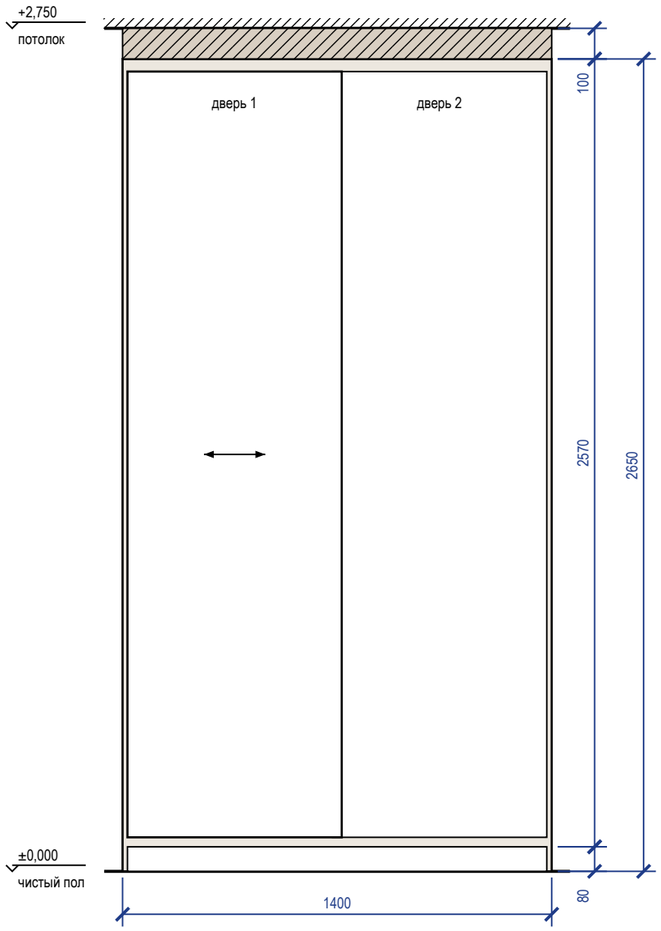


Вид без фасадов

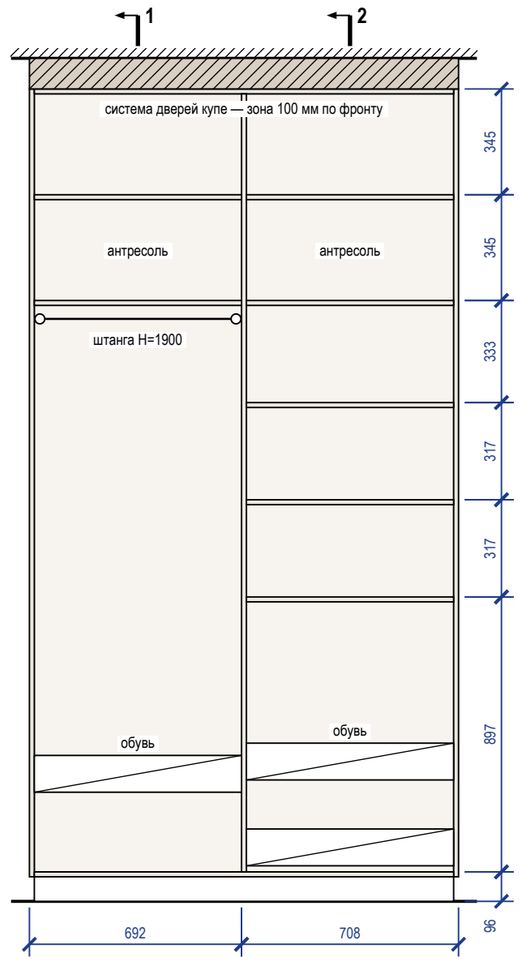

Разрез 1-1

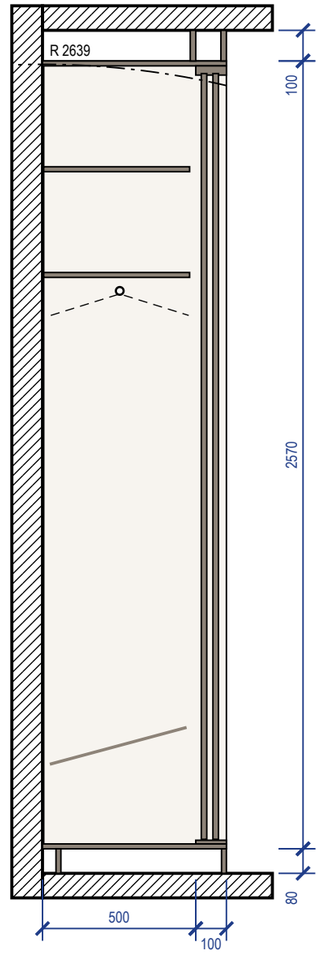


Разрез 2-2

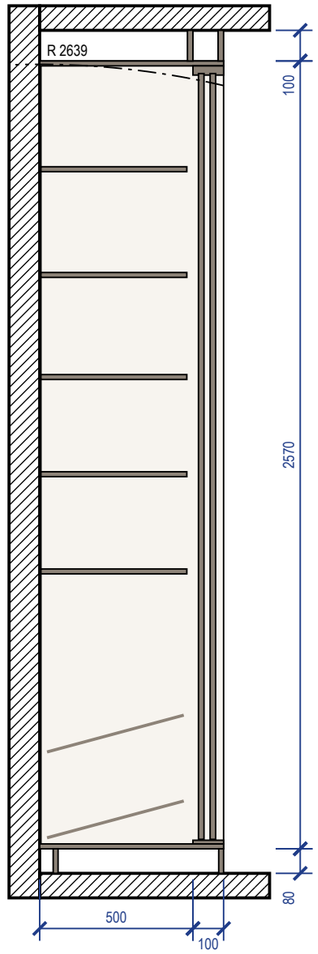

Примечания


1. Размеры — в мм по чистовой отделке; изделие 1400×600×2650 (Ш×Г×В). Перед раскроем — контрольный замер цеха после чистовой отделки стен, пола и потолка.
2. Корпус — ЛДСП 16 мм, задняя стенка ХДФ 4 мм в паз, цоколь 80 мм на регулируемых опорах; двери купе — ЛДСП 10 мм в алюминиевом профиле; нахлёст 30 мм, ширина двери 699 мм, высота — проём минус 40 мм; цвет — по колерной карте.
3. Кромка: скрытые торцы 0,4 мм, видимые 2 мм (ПВХ/АБС).
4. Номинальные зазоры: дверь купе — боковина 3 мм, фасад ящика — стойка 2 мм; ящики внутри купе — с накладкой 30 мм на стойке со стороны нахлёста дверей.
5. Присадка по 32-й системе — выполняет цех.
6. Компенсатор 100 мм — короб из ЛДСП по фронту и торцам, подгоняется к потолку при монтаже (припуск 20 мм), крепится к корпусу и к потолку.
7. Подъём корпуса: диагональ боковины без цоколя $\sqrt{(2570^2 + 600^2)} = 2639$ мм < 2750 мм до потолка — корпус собирается лёжа, поднимается поворотом и ставится на цоколь.
8. Крепление к стене от опрокидывания — уголки 2 шт. к несущему основанию (монтажная схема шкафов).

3D орто

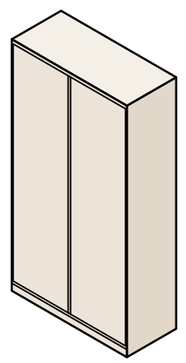


					Проект: Дом 120 м²	**М 1:20**
	Лист	№ док.	Подпись	Дата	Шкаф-купе М_24	Стадия / Лист / Листов
Дизайнер	Кырлан А.С.			04.11.26		П / Д_1 / 136


Вид с фасадами

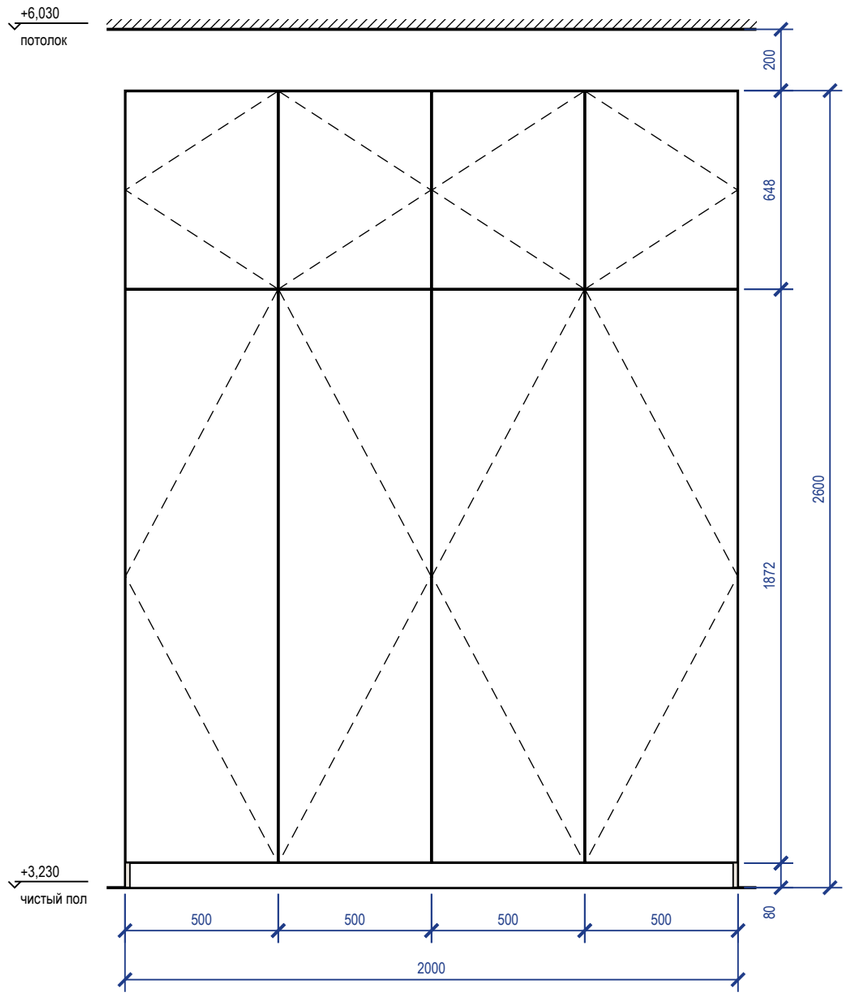


Вид без фасадов

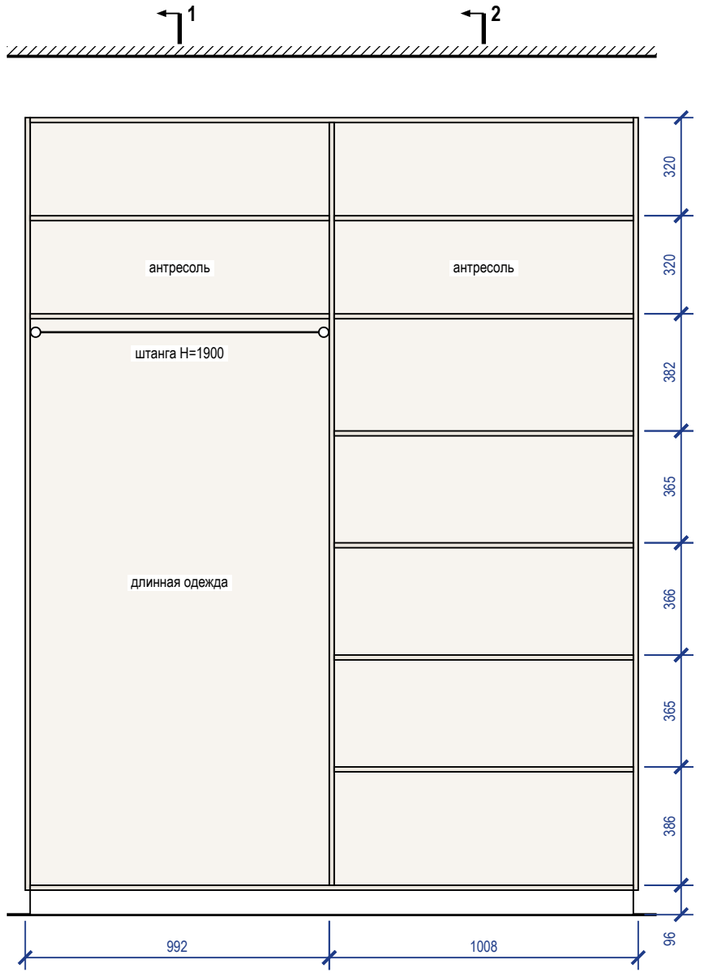

Разрез 1-1

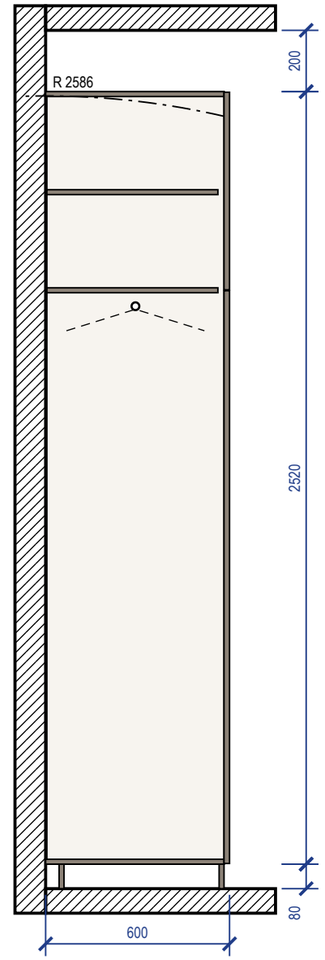


Разрез 2-2

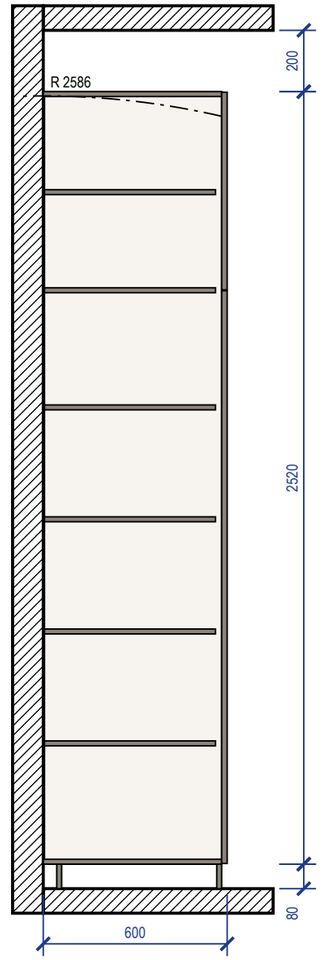

Примечания


1. Размеры — в мм по чистовой отделке; изделие 2000×600×2600 (Ш×Г×В). Перед раскроем — контрольный замер цеха после чистовой отделки стен, пола и потолка.
2. Корпус — ЛДСП 16 мм, задняя стенка ХДФ 4 мм в паз, цоколь 80 мм на регулируемых опорах; фасады накладные — МДФ 18 мм, эмаль матовая, 18 мм; цвет — по колерной карте; петли с доводчиком: фасад 1869 мм — 4 петли, фасад 645 мм — 2 петли.
3. Кромка: скрытые торцы 0,4 мм, видимые 2 мм (ПВХ/АБС).
4. Номинальные зазоры: между фасадами 3 мм, фасад — стена и фасад — потолок не менее 3 мм, фасад ящика — стойка 2 мм.
5. Присадка по 32-й системе — выполняет цех.
6. Зазор до потолка 200 мм.
7. Подъём корпуса: диагональ боковины без цоколя √(2520² + 582²) = 2586 мм < 2800 мм до потолка — корпус собирается лёжа, поднимается поворотом и ставится на цоколь.
8. Крепление к стене от опрокидывания — уголки 2 шт. к несущему основанию (монтажная схема шкафов).

3D орто

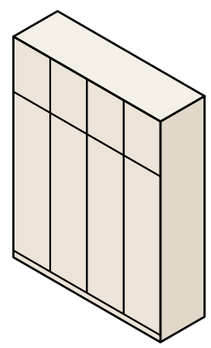


					Проект: Дом 120 м²	М 1:20
	Лист	№ док.	Подпись	Дата		
Дизайнер	Кырлан А.С.			04.11.26	Шкаф распашной М_29	Стадия: П; Лист: Д_2; Листов: 136


Вид с фасадами

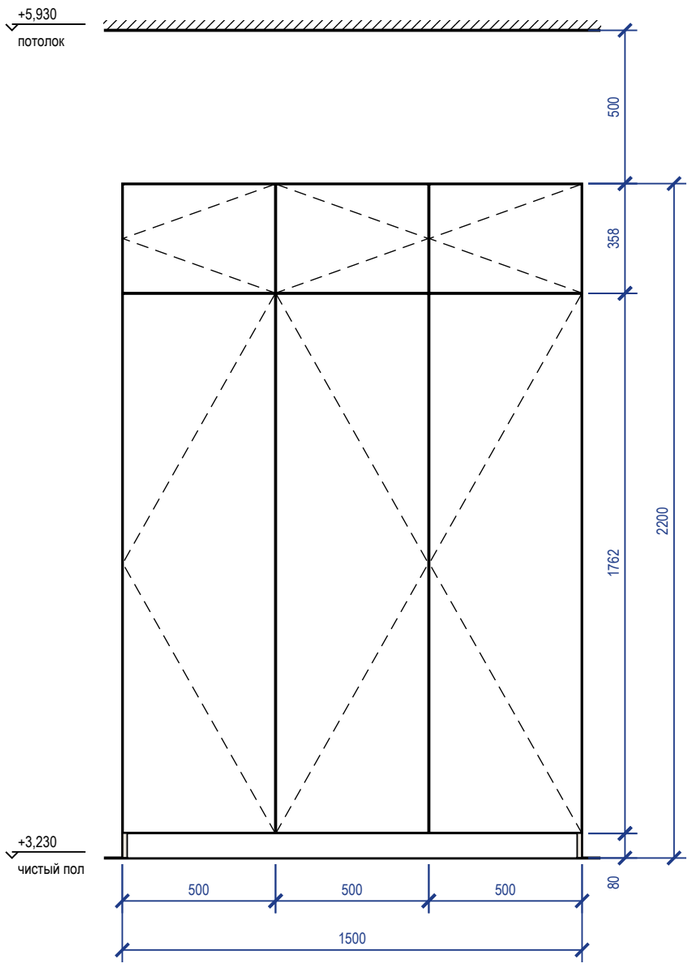


Вид без фасадов

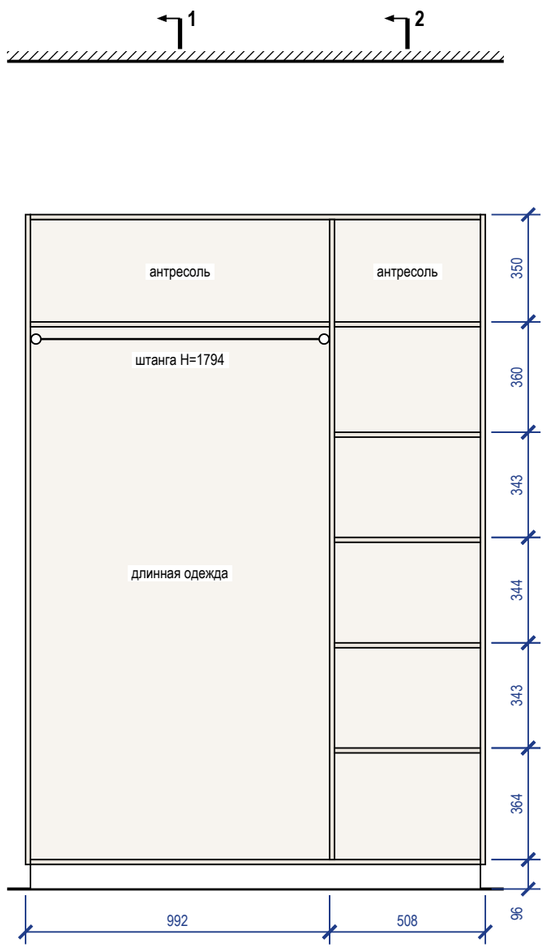

Разрез 1-1

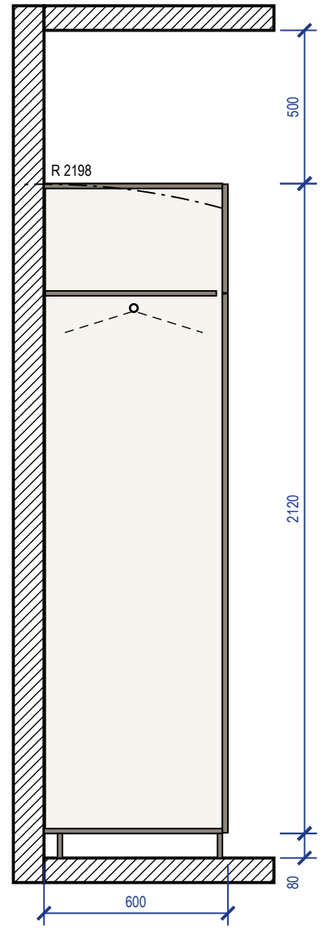


Разрез 2-2

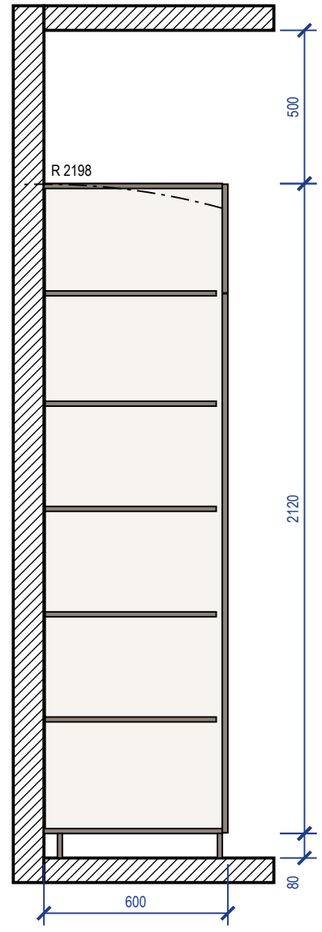

Примечания


1. Размеры — в мм по чистовой отделке; изделие 1500×600×2200 (Ш×Г×В). Перед раскроем — контрольный замер цеха после чистовой отделки стен, пола и потолка.
2. Корпус — ЛДСП 16 мм, задняя стенка ХДФ 4 мм в паз, цоколь 80 мм на регулируемых опорах; фасады накладные — МДФ 18 мм, эмаль матовая, 18 мм; цвет — по колерной карте; петли с доводчиком: фасад 1759 мм — 4 петли, фасад 355 мм — 2 петли.
3. Кромка: скрытые торцы 0,4 мм, видимые 2 мм (ПВХ/АБС).
4. Номинальные зазоры: между фасадами 3 мм, фасад — стена и фасад — потолок не менее 3 мм, фасад ящика — стойка 2 мм.
5. Присадка по 32-й системе — выполняет цех.
6. Зазор до потолка 500 мм.
7. Подъём корпуса: диагональ боковины без цоколя $\sqrt{(2120^2 + 582^2)} = 2198$ мм < 2700 мм до потолка — корпус собирается лёжа, поднимается поворотом и ставится на цоколь.
8. Крепление к стене от опрокидывания — уголки 2 шт. к несущему основанию (монтажная схема шкафов).

3D орто

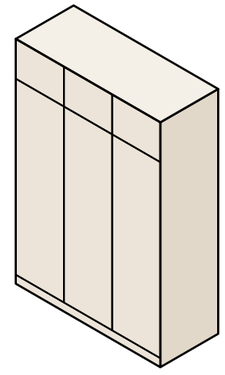


					Проект: Дом 120 м²	**М 1:20**
	Лист	№ док.	Подпись	Дата	Шкаф распашной М_34	Стадия / Лист / Листов
Дизайнер	Кырлан А.С.			04.11.26		П / Д_3 / 136


Общий вид

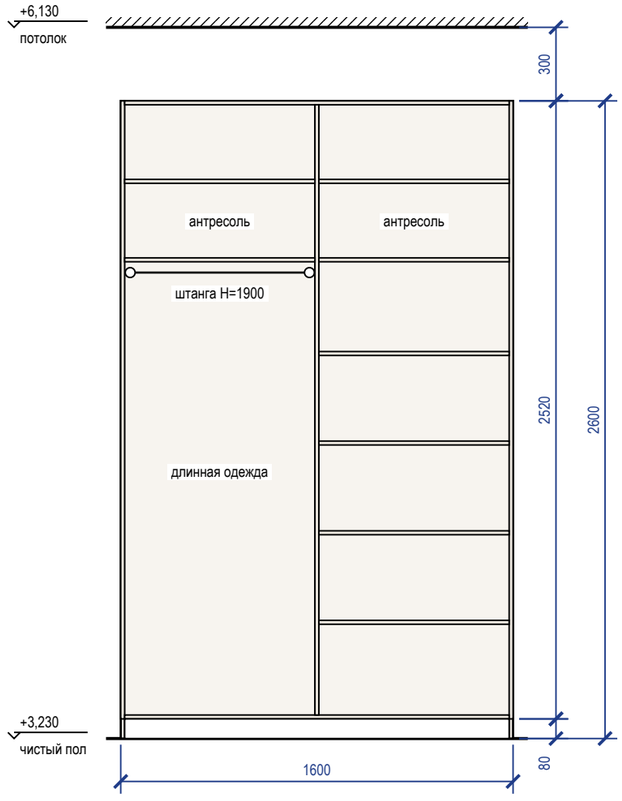


Наполнение, размеры в свету

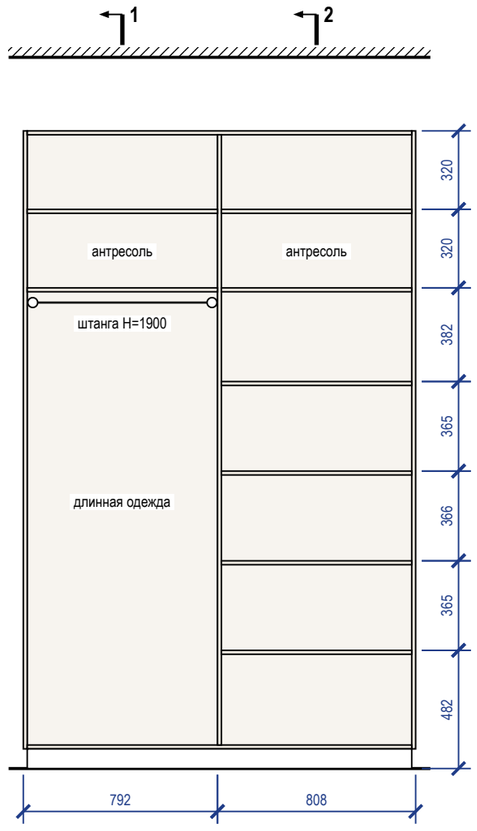

Разрез 1-1

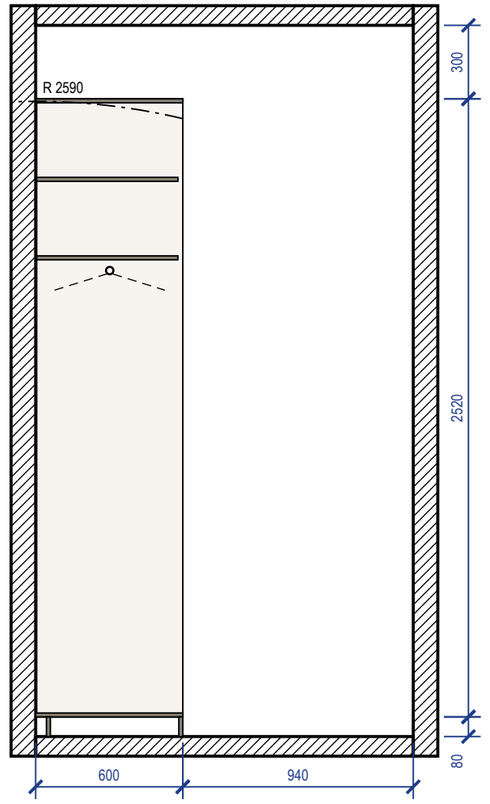


Разрез 2-2

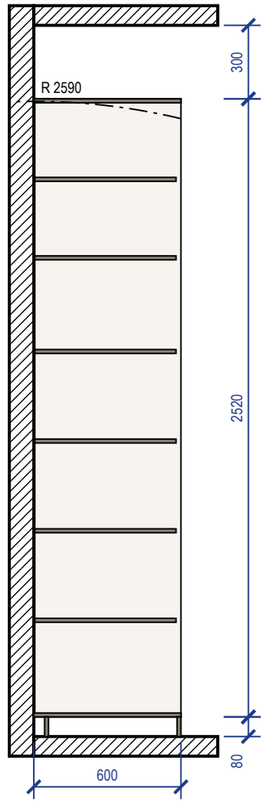

Примечания


1. Размеры — в мм по чистовой отделке; изделие 1600×600×2600 (Ш×Г×В). Перед раскроем — контрольный замер цеха после чистовой отделки стен, пола и потолка.
2. Корпус — ЛДСП 16 мм, задняя стенка ХДФ 4 мм в паз, цоколь 80 мм на регулируемых опорах; открытая система: без фасадов.
3. Кромка: скрытые торцы 0,4 мм, видимые 2 мм (ПВХ/АБС).
4. Присадка по 32-й системе — выполняет цех.
5. Зазор до потолка 300 мм.
6. Подъём корпуса: диагональ боковины без цоколя √(2520² + 600²) = 2590 мм < 2900 мм до потолка — корпус собирается лёжа, поднимается поворотом и ставится на цоколь.
7. Крепление к стене от опрокидывания — уголки 2 шт. к несущему основанию (монтажная схема шкафов).
8. Проход перед изделием 940 мм показан на разрезе 1-1.

3D орто

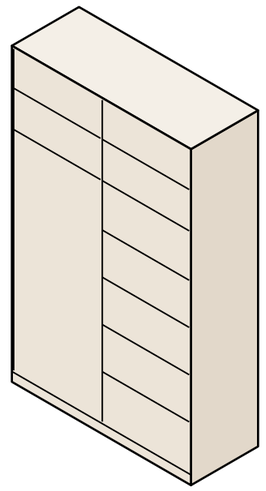


					Проект: Дом 120 м²		M 1:25
	Лист	№ док.	Подпись	Дата	Система хранения M_37	Стадия	Лист	Листов
Дизайнер	Кырлан А.С.			04.11.26		П	Д_4	136


Общий вид

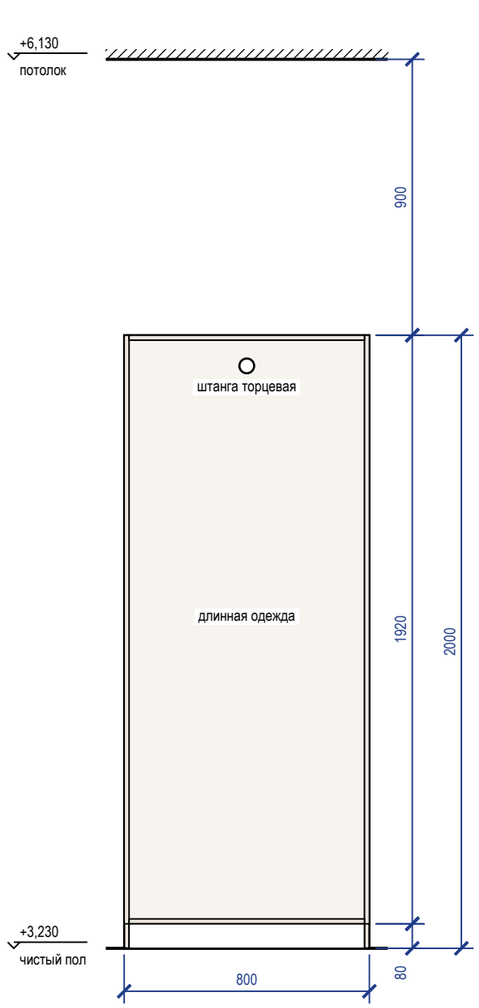

Наполнение, размеры в свету

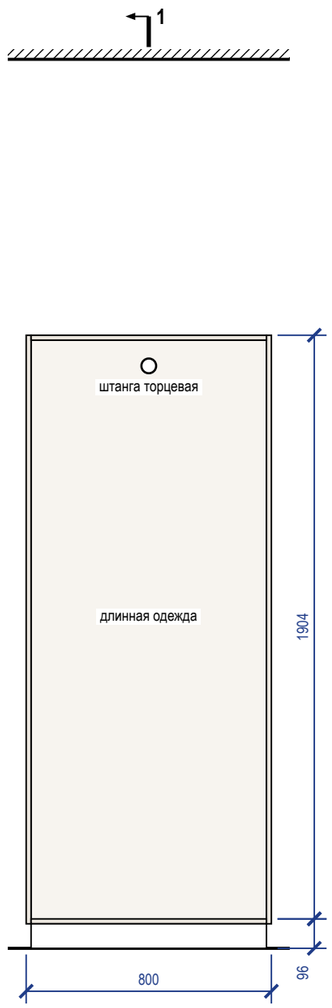


Разрез 1-1

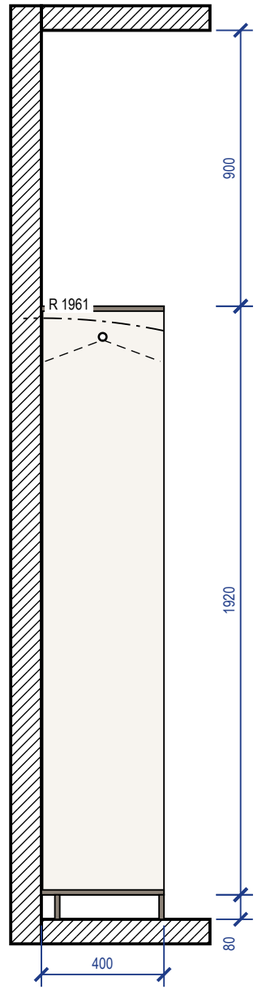

Примечания


1. Размеры — в мм по чистовой отделке; изделие 800×400×2000 (Ш×Г×В). Перед раскроем — контрольный замер цеха после чистовой отделки стен, пола и потолка.
2. Корпус — ЛДСП 16 мм, задняя стенка ХДФ 4 мм в паз, цоколь 80 мм на регулируемых опорах; открытая система: без фасадов.
3. Кромка: скрытые торцы 0,4 мм, видимые 2 мм (ПВХ/АБС).
4. Присадка по 32-й системе — выполняет цех.
5. Зазор до потолка 900 мм.
6. Подъём корпуса: диагональ боковины без цоколя $\sqrt{(1920^2 + 400^2)} = 1961$ мм < 2900 мм до потолка — корпус собирается лёжа, поднимается поворотом и ставится на цоколь.
7. Крепление к стене от опрокидывания — уголки 2 шт. к несущему основанию (монтажная схема шкафов).

3D орто

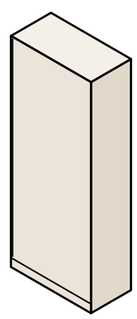


					Проект: Дом 120 м²	**М 1:20**
	Лист	№ док.	Подпись	Дата	Система хранения М_38	Стадия / Лист / Листов
Дизайнер	Кырлан А.С.			04.11.26		П / Д_5 / 136


Общий вид

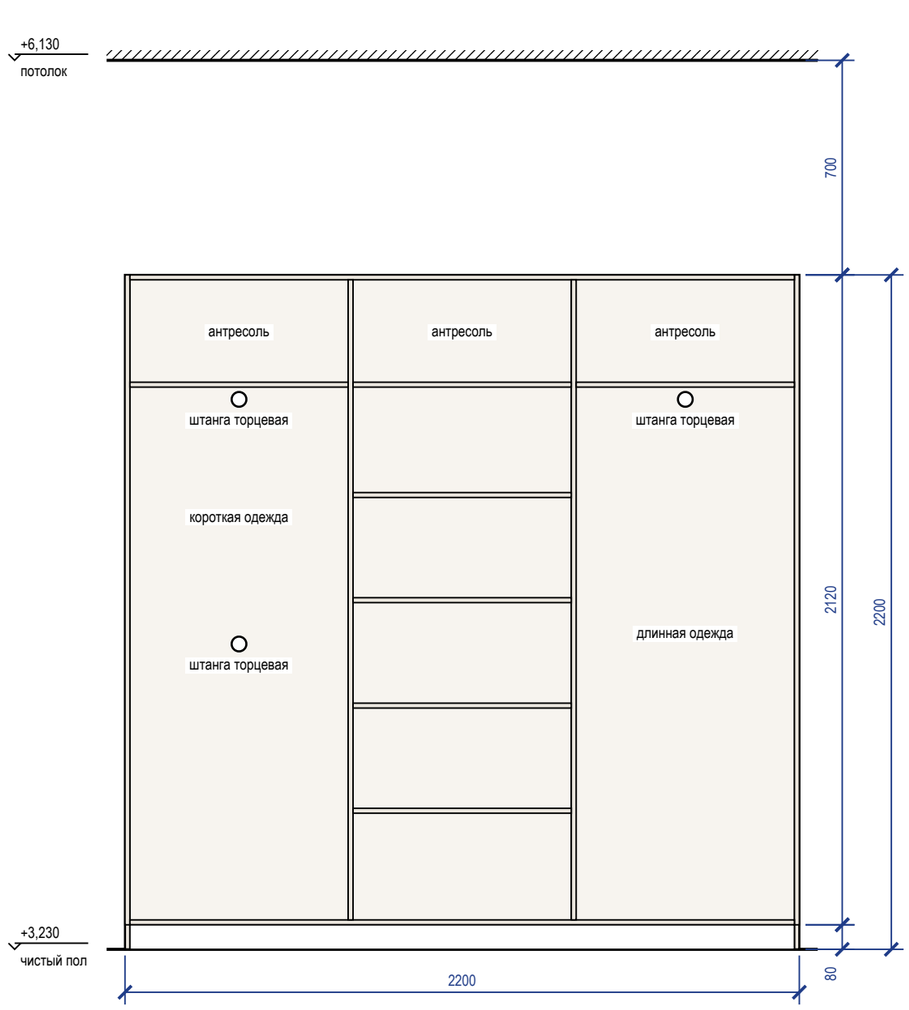


Наполнение, размеры в свету

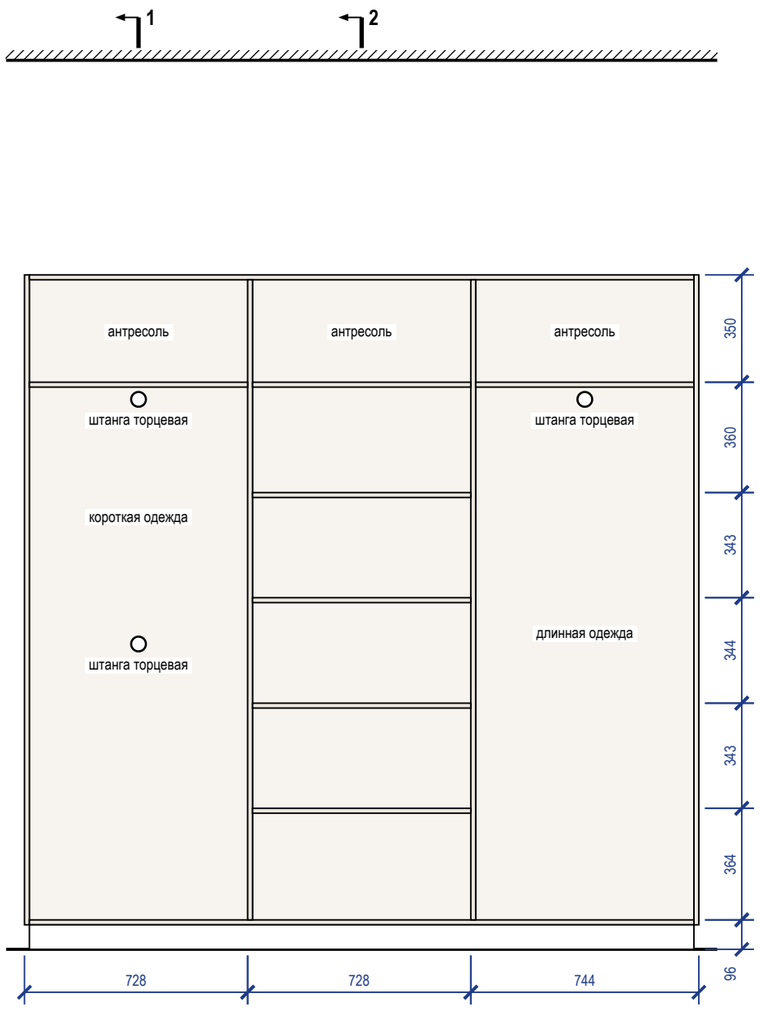

Разрез 1-1

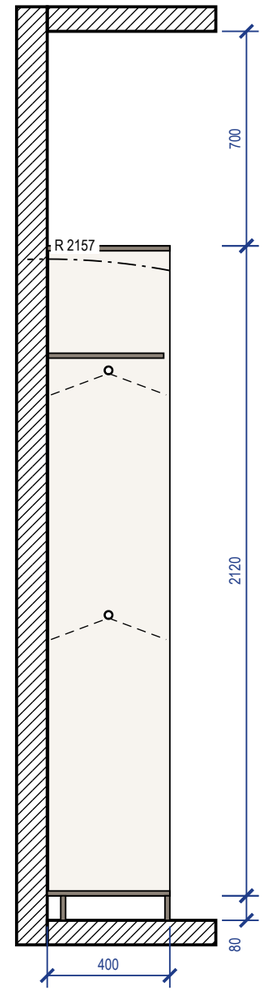


Разрез 2-2

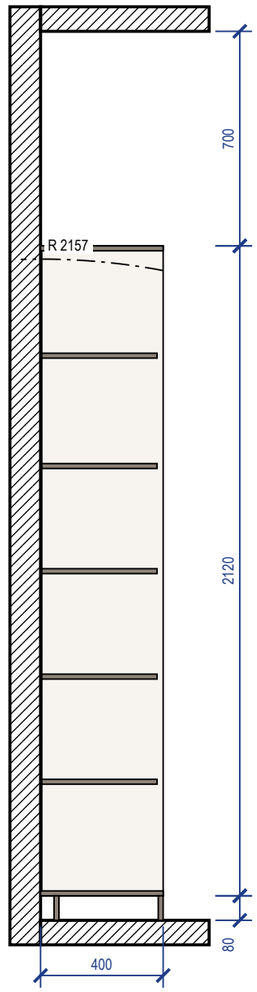

Примечания

1. Размеры — в мм по чистовой отделке; изделие 2200×400×2200 (Ш×Г×В). Перед раскроем — контрольный замер цеха после чистовой отделки стен, пола и потолка.
2. Корпус — ЛДСП 16 мм, задняя стенка ХДФ 4 мм в паз, цоколь 80 мм на регулируемых опорах; открытая система: без фасадов.
3. Кромка: скрытые торцы 0,4 мм, видимые 2 мм (ПВХ/АБС).
4. Присадка по 32-й системе — выполняет цех.
5. Зазор до потолка 700 мм.
6. Подъём корпуса: диагональ боковины без цоколя $\sqrt{(2120^2 + 400^2)} = 2157$ мм < 2900 мм до потолка — корпус собирается лёжа, поднимается поворотом и ставится на цоколь.
7. Крепление к стене от опрокидывания — уголки 2 шт. к несущему основанию (монтажная схема шкафов).


3D орто

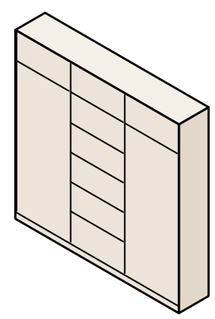


					Проект: Дом 120 м²	**М 1:20**
	Лист	№ док.	Подпись	Дата	Система хранения М_39	Стадия / Лист / Листов
Дизайнер	Кырлан А.С.			04.11.26		П / Д_6 / 136

выпуск 04.11.2026 № 406ed8a6ce · стр. 123 из 136


Общий вид

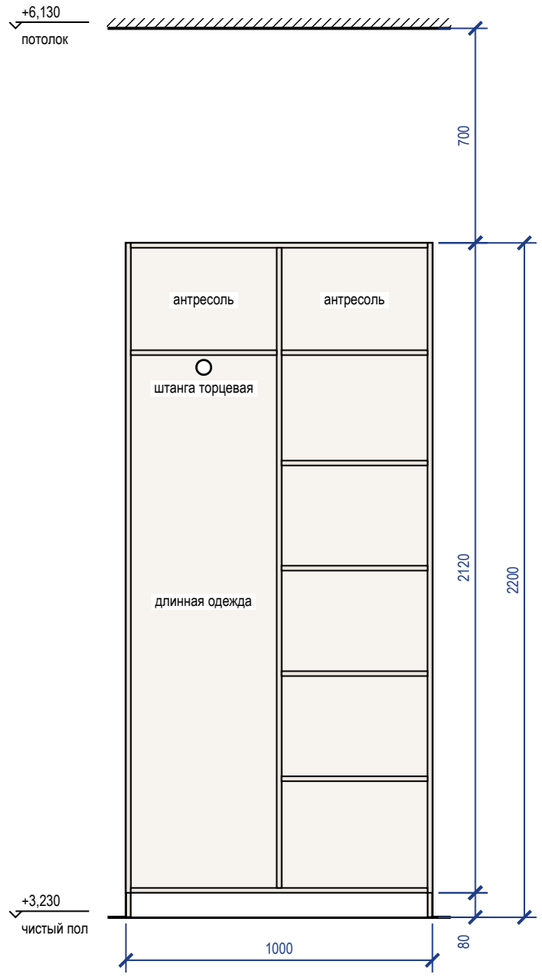


Наполнение, размеры в свету

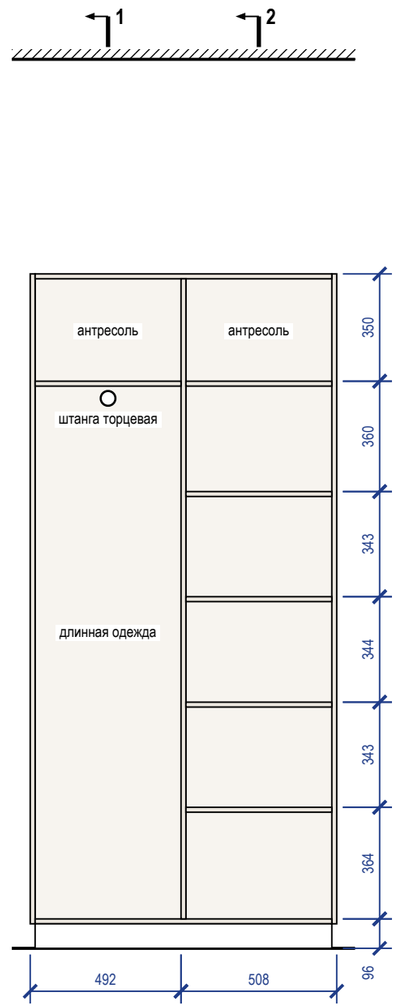

Разрез 1-1

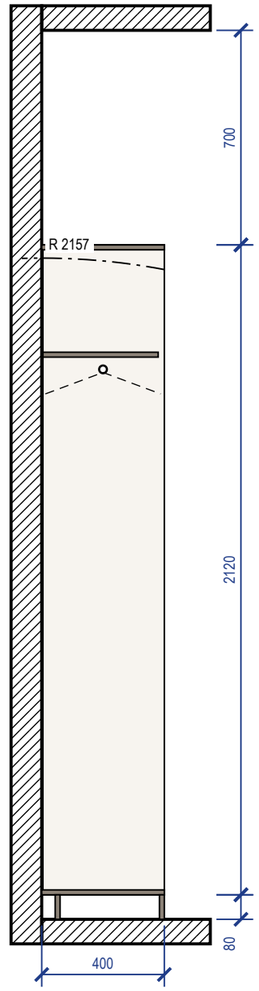


Разрез 2-2

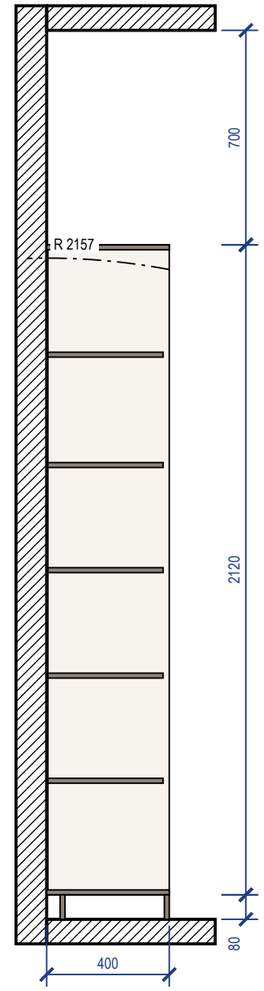

Примечания

1. Размеры — в мм по чистовой отделке; изделие 1000×400×2200 (Ш×Г×В). Перед раскроем — контрольный замер цеха после чистовой отделки стен, пола и потолка.
2. Корпус — ЛДСП 16 мм, задняя стенка ХДФ 4 мм в паз, цоколь 80 мм на регулируемых опорах; открытая система: без фасадов.
3. Кромка: скрытые торцы 0,4 мм, видимые 2 мм (ПВХ/АБС).
4. Присадка по 32-й системе — выполняет цех.
5. Зазор до потолка 700 мм.
6. Подъём корпуса: диагональ боковины без цоколя $\sqrt{(2120^2 + 400^2)} = 2157$ мм < 2900 мм до потолка — корпус собирается лёжа, поднимается поворотом и ставится на цоколь.
7. Крепление к стене от опрокидывания — уголки 2 шт. к несущему основанию (монтажная схема шкафов).


3D орто

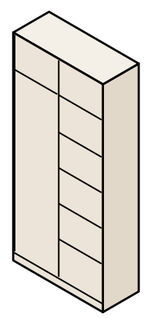


					Проект: Дом 120 м²	**М 1:20**
	Лист	№ док.	Подпись	Дата	Система хранения M_40	
Дизайнер	Кырлан А.С.			04.11.26		

Стадия	Лист	Листов
П	Д_7	136


Вид с фасадами

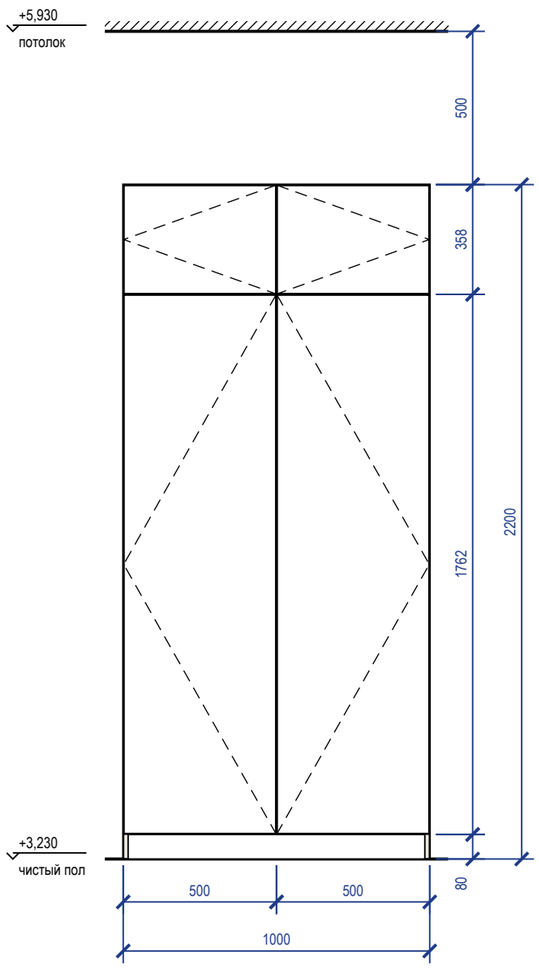

Вид без фасадов

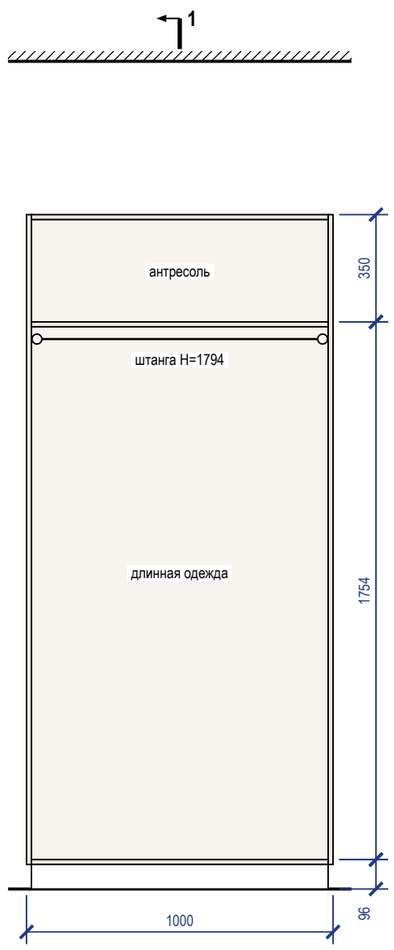


Разрез 1-1

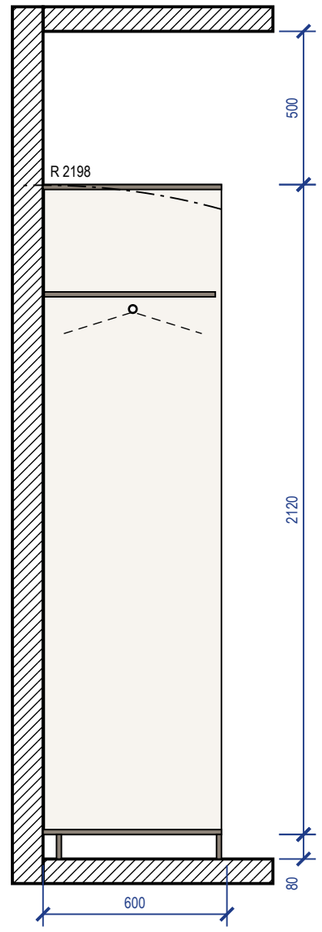

Примечания


1. Размеры — в мм по чистовой отделке; изделие 1000×600×2200 (Ш×Г×В). Перед раскроем — контрольный замер цеха после чистовой отделки стен, пола и потолка.
2. Корпус — ЛДСП 16 мм, задняя стенка ХДФ 4 мм в паз, цоколь 80 мм на регулируемых опорах; фасады накладные — МДФ 18 мм, эмаль матовая, 18 мм; цвет — по колерной карте; петли с доводчиком: фасад 1759 мм — 4 петли, фасад 355 мм — 2 петли.
3. Кромка: скрытые торцы 0,4 мм, видимые 2 мм (ПВХ/АБС).
4. Номинальные зазоры: между фасадами 3 мм, фасад — стена и фасад — потолок не менее 3 мм, фасад ящика — стойка 2 мм.
5. Присадка по 32-й системе — выполняет цех.
6. Зазор до потолка 500 мм.
7. Подъём корпуса: диагональ боковины без цоколя $\sqrt{(2120^2 + 582^2)} = 2198$ мм < 2700 мм до потолка — корпус собирается лёжа, поднимается поворотом и ставится на цоколь.
8. Крепление к стене от опрокидывания — уголки 2 шт. к несущему основанию (монтажная схема шкафов).

3D орто

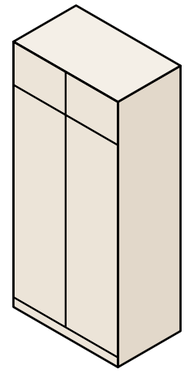


					Проект: Дом 120 м²		M 1:20
	Лист	№ док.	Подпись	Дата			
Дизайнер	Кырлан А.С.			04.11.26	Шкаф распашной М_44	Стадия / Лист / Листов	
						П / Д_8 / 136	


Общий вид

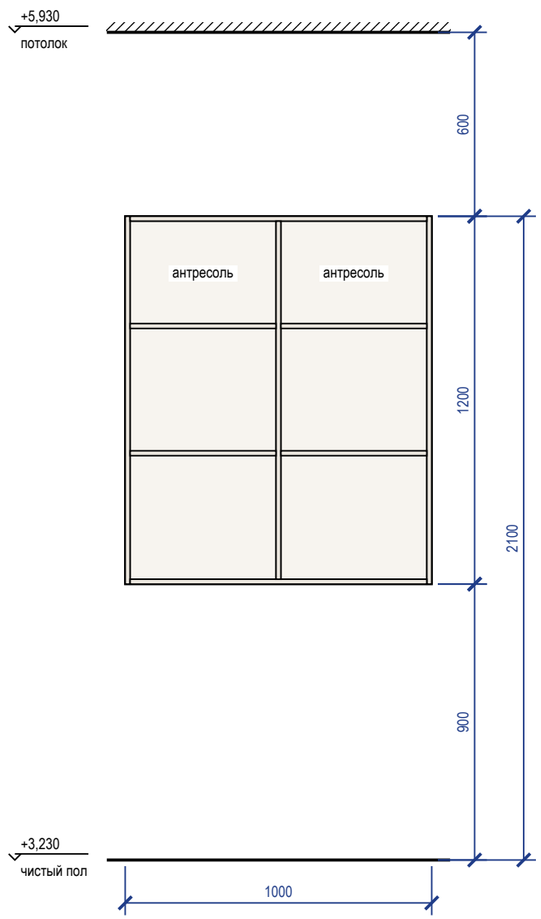

Наполнение, размеры в свету

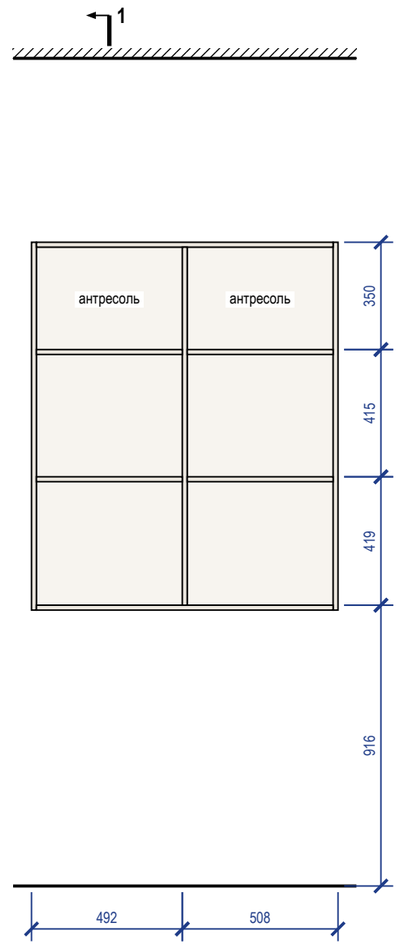


Разрез 1-1

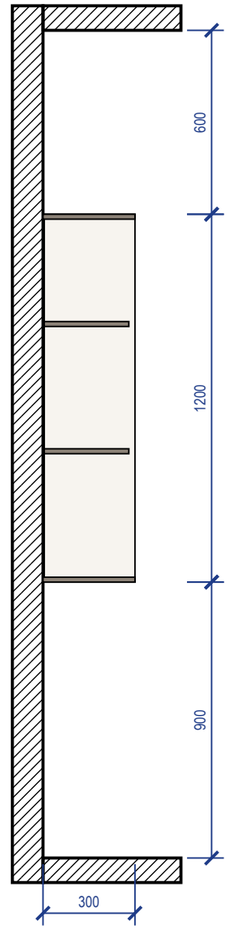

Примечания

1. Размеры — в мм по чистовой отделке; изделие 1000×300×1200 (Ш×Г×В). Перед раскроем — контрольный замер цеха после чистовой отделки стен, пола и потолка.
2. Корпус — ЛДСП 16 мм, задняя стенка ХДФ 4 мм в паз, навесной корпус без цоколя, низ на 900 мм от чистого пола; открытая система: без фасадов.
3. Кромка: скрытые торцы 0,4 мм, видимые 2 мм (ПВХ/АБС).
4. Присадка по 32-й системе — выполняет цех.
5. Зазор до потолка 600 мм.
6. Навесной корпус — на стене: регулируемые навесы на монтажную шину или анкеры в несущее основание; основание стены и шаг анкеров — монтажная схема шкафов.


3D орто

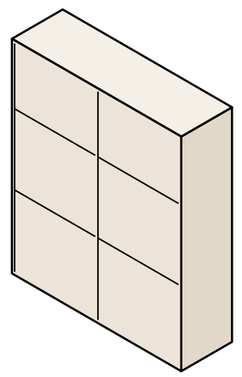


					Проект: Дом 120 м²	**М 1:20**
	Лист	№ док.	Подпись	Дата		
Дизайнер	Кырлан А.С.			04.11.26	Система хранения М_46	Стадия / Лист / Листов
						П / Д_9 / 136

выпуск 04.11.2026 № 406ed8a6ce · стр. 126 из 136


Вид с фасадами

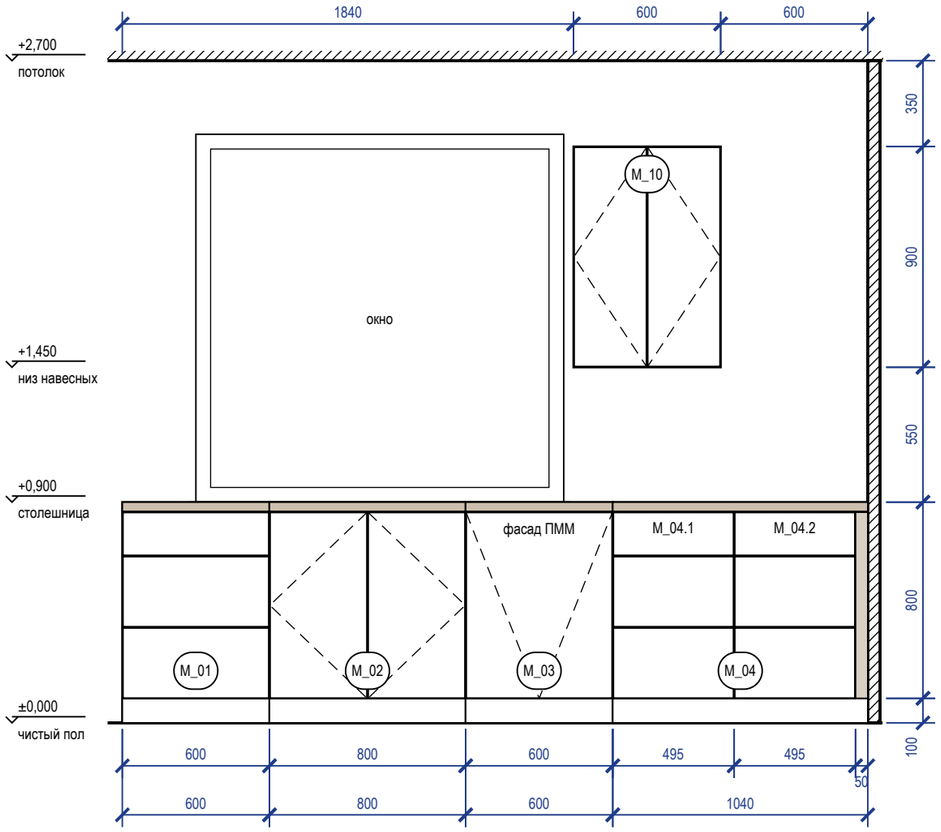


Вид без фасадов (наполнение, выводы)

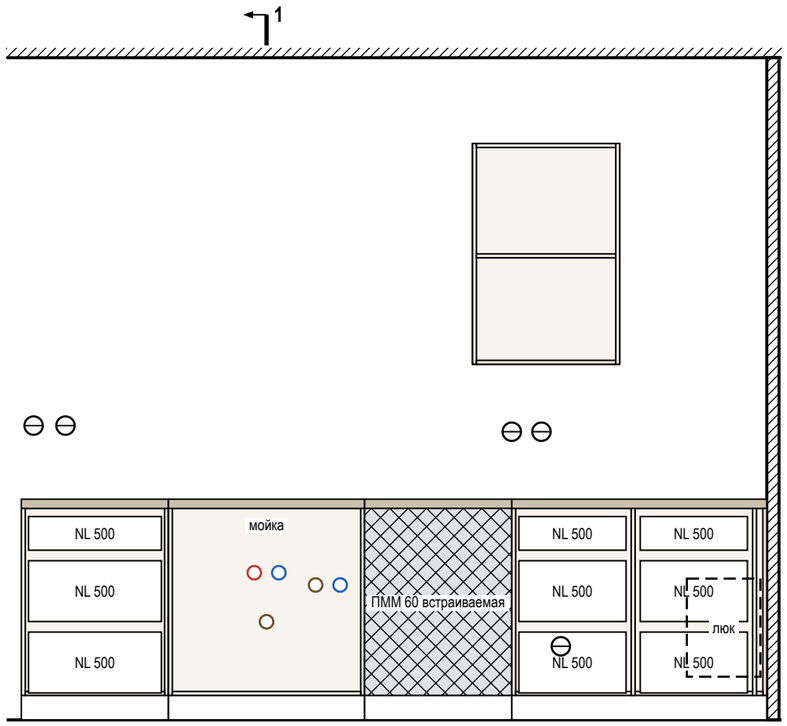

Разрез 1-1

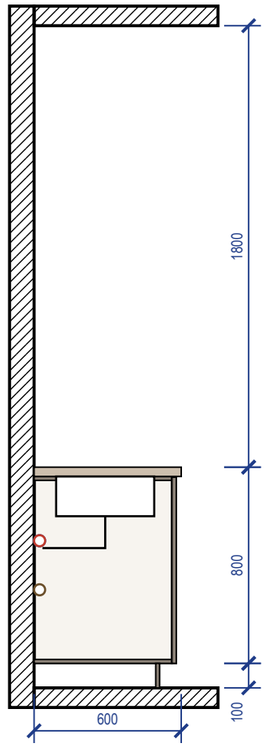

3D орто

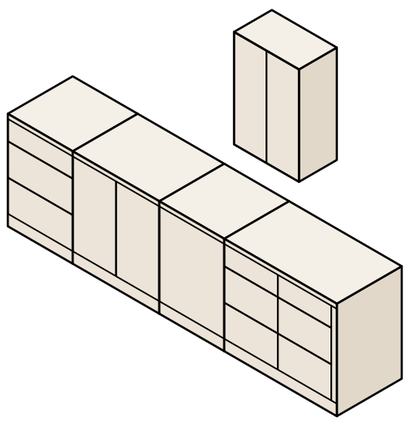

Примечания

1. Размеры — в мм по чистовой отделке, вид из помещения; марки — как на плане расстановки. Перед раскроем — контрольный замер цеха после фартука и пола.
2. Корпуса — ЛДСП 16 мм, задняя стенка ХДФ 4 мм; фасады — МДФ, эмаль матовая 18 мм, цвет по колерной карте; столешница 38 мм, свес 20 мм; цоколь 100 мм.
3. Кромка: скрытые торцы 0,4 мм, видимые 2 мм. Номинальные зазоры: между фасадами 3 мм, фасад — столешница 3 мм, фасад — стена не менее 3 мм.
4. Ящики полного выдвижения и петли — с доводчиком; присадка по 32-й системе — выполняет цех.
5. Ниши техники — по монтажным схемам выбранных моделей: решётка в цоколе и канал за пеналом холодильника, зазор за духовым шкафом, фасад ПММ на двери машины.
6. M_04: сервисный люк к стоякам Ст К1-2 (кухня), Ст В1-2, Ст Т3-2 — съёмная панель 300×400 мм в задней стенке на саморезах (по виду без фасадов, штриховой контур «люк»), доступ через фасад модуля; короб стояков за модулем — с ревизией напротив люка (лист ВК).

	Лист	№ док.	Подпись	Дата
Дизайнер	Кырлан А.С.			04.11.26


Проект: Дом 120 м² — **М 1:25**

Кухня (пом. 1). Развёртка гарнитура


Стадия	Лист	Листов
П	Д_10	136

выпуск 04.11.2026 № 406ed8a6ce · стр. 127 из 136


Вид с фасадами

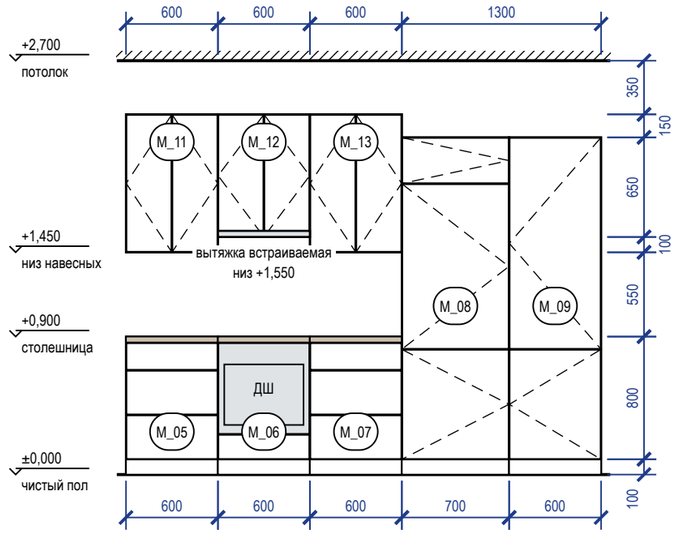


Вид без фасадов (наполнение, выводы)

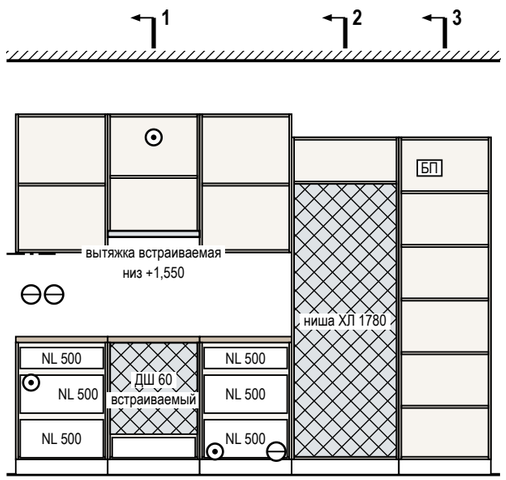


Разрез 1-1

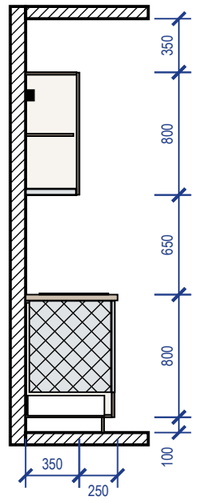


Разрез 2-2

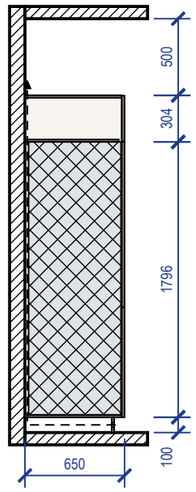

Разрез 3-3

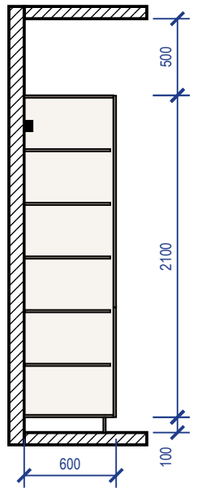

3D орто

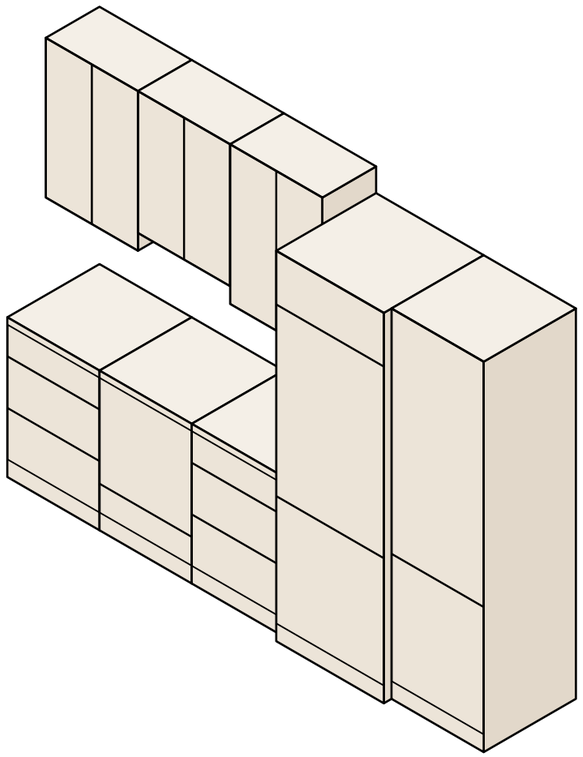

Примечания

1. Размеры — в мм по чистовой отделке, вид из помещения; марки — как на плане расстановки. Перед раскроем — контрольный замер цеха после фартука и пола.
2. Корпуса — ЛДСП 16 мм, задняя стенка ХДФ 4 мм; фасады — МДФ, эмаль матовая 18 мм, цвет по колерной карте; столешница 38 мм, свес 20 мм; цоколь 100 мм.
3. Кромка: скрытые торцы 0,4 мм, видимые 2 мм. Номинальные зазоры: между фасадами 3 мм, фасад — столешница 3 мм, фасад — стена не менее 3 мм.
4. Ящики полного выдвижения и петли — с доводчиком; присадка по 32-й системе — выполняет цех.
5. Вытяжка встраивается в дно навесного модуля M_12 над варочной: её низ на 1550 мм от пола, 650 мм над панелью (не меньше 650 мм).
6. Ниши техники (холодильник — ориентир 1780 мм) — по монтажным схемам выбранных моделей: решётка в цоколе и канал за пеналом холодильника, зазор за духовым шкафом, фасад ПММ на двери машины.

					Проект: Дом 120 м²		**М 1:40**
	Лист	№ док.	Подпись	Дата	Кухня (пом. 1). Развёртка гарнитура	Стадия	Лист	Листов
Дизайнер	Кырлан А.С.			04.11.26		П	Д_11	136

Ведомость отделки помещений (форма 1 прил. А ГОСТ 21.501-2018). Лист 1 из 3

№	Наименование помещения	Потолок			Стены и перегородки			Низ стен (плинтус)			Пол		Примечание
		Вид отделки	Код цвета	S, м²	Вид отделки	Код цвета	S, м²	Вид отделки	Код цвета	L, м	Вид отделки	S, м²	
1	Гостиная-кухня 31,32 м²	ГКЛ по каркасу П113, отм. +2,700; +2,800; +2,750; окраска, Little Greene Absolute Matt, глубокоматовая, 2 слоя, подготовка Q3	Little Greene No. 222	31,32	Окраска, Tikkurila, матовая, 2 слоя, подготовка Q3 Акцент — стена А: окраска, Tikkurila, матовая, 2 слоя, подготовка Q3 Фартук кухни (стена А, Б): облицовка керамогранитом, аналог: керамогранит под травертин, матовый, 1200×600×9 мм, клей C2 TE S1, затирка CG2WA	Tikkurila G503 NCS S 3050-R80B по артикулу	39,96 10,31 1,94	Плинтус МДФ h=80 мм, аналог: МДФ под покраску 80×16	Tikkurila G503	21,7	Инженерная доска, 1167-4250, 2100×127 мм, на клею; тип 1, отм. ЧП ±0,000	31,32	Н стен 2700 (до потолка); матовая моющаяся, класс 1 EN 13300 — осознанно вместо полуматовой; краска бренда веера G503 — Tikkurila матовая линейка класса 1 — по каталогу Tikkurila при закупке; краска бренда веера Little Greene; класс по EN 13300 и блеск линейки — по ТУ Little Greene, в базе не сверены; плинтус в цвет: стены
2	Холл с лестницей 15,51 м²	ГКЛ по каркасу П113, отм. +2,800; окраска, Little Greene Absolute Matt, глубокоматовая, 2 слоя, подготовка Q3	Little Greene No. 222	15,51	Окраска, Tikkurila, матовая, 2 слоя, подготовка Q3	Tikkurila G503	33,04	Плинтус МДФ h=80 мм, аналог: МДФ под покраску 80×16	Tikkurila G503	11,1	Инженерная доска, 1167-4250, 2100×127 мм, на клею; тип 1, отм. ЧП ±0,000	15,51	Н стен 2800 (до потолка); матовая моющаяся, класс 1 EN 13300 — осознанно вместо полуматовой; краска бренда веера G503 — Tikkurila матовая линейка класса 1 — по каталогу Tikkurila при закупке; краска бренда веера Little Greene; класс по EN 13300 и блеск линейки — по ТУ Little Greene, в базе не сверены; плинтус в цвет: стены
3	Кабинет 11,00 м²	ГКЛ по каркасу П113, отм. +2,800; +2,650; окраска, Little Greene Absolute Matt, глубокоматовая, 2 слоя, подготовка Q3	Little Greene No. 222	11,00	Окраска, Tikkurila, матовая, 2 слоя, подготовка Q3 Акцент — стена А: окраска, Tikkurila, матовая, 2 слоя, подготовка Q3	Tikkurila G503 NCS S 5020-G90Y	23,01 10,47	Плинтус МДФ h=80 мм, аналог: МДФ под покраску 80×16	Tikkurila G503	12,6	Инженерная доска, 1167-4250, 2100×127 мм, на клею; тип 1, отм. ЧП ±0,000	11,00	Н стен 2800 (до потолка); краска бренда веера G503 Tikkurila; матовая линейка класса 1 — по каталогу Tikkurila при закупке; краска бренда веера Little Greene класс по EN 13300 и блеск линейки — по ТУ Little Greene, в базе не сверены; плинтус в цвет: стены
4	Санузел гостевой 4,17 м²	ГКЛВ по каркасу П113, отм. +2,600; окраска, Little Greene Intelligent Bathroom, матовая, 2 слоя, подготовка Q3	Little Greene No. 222	4,17	Облицовка плиткой, A8UZ, 600×1200×9 мм, клей C2 TE S1, затирка CG2WA	Atlas Concorde A8UZ	17,40	нет			Аналог: керамогранит ректифицированный под травертин, матовый, 600×600×9 мм; тип 2, отм. ЧП −0,015	4,17	Н стен 2615 (до потолка); гидроизоляция обмазочная, 2 слоя, с заведением на стены 200 мм (по пирогу пола); тест проливом и акт скрытых работ; краска бренда веера Little Greene; класс по EN 13300 и блеск линейки — по ТУ Little Greene, в базе не сверены

Примечания

1. Ведомость продолжена на листе 2 из 3; итоги, сводка площадей и примечания — на последнем листе ведомости.

					Проект: Дом 120 м²
	Лист	№ док.	Подпись	Дата	Ведомость отделки помещений. Лист 1 из 3
Дизайнер	Кырлан А.С.			04.11.26	

Стадия	Лист	Листов
П	С1	136

Ведомость отделки помещений (форма 1 прил. А ГОСТ 21.501-2018). Лист 2 из 3

№	Наименование помещения	Потолок			Стены и перегородки			Низ стен (плинтус)			Пол		Примечание
		Вид отделки	Код цвета	S, м²	Вид отделки	Код цвета	S, м²	Вид отделки	Код цвета	L, м	Вид отделки	S, м²	
5	Прихожая 12,20 м²	ГКЛ по каркасу П113, отм. +2,750; окраска, Little Greene Absolute Matt, глубокоматовая, 2 слоя, подготовка Q3	Little Greene No. 222	12,20	Окраска, Tikkurila, матовая, 2 слоя, подготовка Q3	Tikkurila G503	40,60	Плинтус МДФ h=80 мм, аналог: МДФ под покраску 80×16	Tikkurila G503	14,0	Керамогранит, A8UZ, 600×1200×9 мм; тип 3, отм. ЧП ±0,000	12,20	Н стен 2750 (до потолка); матовая моющаяся, класс 1 EN 13300 — осознанно вместо полуматовой; краска бренда веера G503 — Tikkurila матовая линейка класса 1 — по каталогу Tikkurila при закупке; краска бренда веера Little Greene; класс по EN 13300 и блеск линейки — по ТУ Little Greene, в базе не сверены; плинтус в цвет: стены
6	Спальня родителей 17,17 м²	ГКЛ по каркасу П113, отм. +6,030; +5,880; окраска, Little Greene Absolute Matt, глубокоматовая, 2 слоя, подготовка Q3	Little Greene No. 222	17,17	Окраска, Tikkurila, матовая, 2 слоя, подготовка Q3 Акцент — стена А: окраска, Farrow & Ball Modern Emulsion, матовая, 2 слоя, подготовка Q3	Tikkurila G503 Farrow & Ball No. 89	32,56 7,21	Плинтус МДФ h=80 мм, аналог: МДФ под покраску 80×16	Tikkurila G503	15,9	Инженерная доска, 1167-4250, 2100×127 мм, на клею; тип 1, отм. ЧП +3,230	17,17	Н стен 2650 (до потолка); краска бренда веера G503 Tikkurila; матовая линейка класса 1 — по каталогу Tikkurila при закупке; краска бренда веера Little Greene класс по EN 13300 и блеск линейки — по ТУ Little Greene, в базе не сверены; плинтус в цвет: стены
7	Детская 12,30 м²	ГКЛ по каркасу П113, отм. +5,930; +6,030; окраска, Little Greene Absolute Matt, глубокоматовая, 2 слоя, подготовка Q3	Little Greene No. 222	12,30	Окраска, Tikkurila, полуматовая, 2 слоя, подготовка Q3 Акцент — стена А: окраска, Farrow & Ball, полуматовая, 2 слоя, подготовка Q3	Tikkurila G503 Farrow & Ball No. 66	24,01 10,10	Плинтус МДФ h=69 мм, SX165	Tikkurila G503	13,3	Инженерная доска, 1167-4250, 2100×127 мм, на клею; тип 1, отм. ЧП +3,230	12,30	Н стен 2700 (до потолка); краска бренда веера Little Greene; класс по EN 13300 и блеск линейки — по ТУ Little Greene, в базе не сверены; плинтус в цвет: стены
8	Гардеробная 3,82 м²	Потолок под покраску, отм. +6,130; окраска, Little Greene Absolute Matt, глубокоматовая, 2 слоя, подготовка Q3	Little Greene No. 222	3,82	Окраска, Little Greene Intelligent Matt, матовая, 2 слоя, подготовка Q3	Little Greene No. 222	22,06	Плинтус МДФ h=80 мм, аналог: МДФ под покраску 80×16	Little Greene No. 222	7,4	Инженерная доска, 1167-4250, 2100×127 мм, на клею; тип 1, отм. ЧП +3,230	3,82	Н стен 2900 (до потолка); краска бренда веера Little Greene; класс по EN 13300 и блеск линейки — по ТУ Little Greene, в базе не сверены; краска бренда веера Little Greene класс по EN 13300 и блеск линейки — по ТУ Little Greene, в базе не сверены; плинтус в цвет: стены
9	Кладовая 4,66 м²	Потолок под покраску, отм. +6,130; окраска, Tikkurila, глубокоматовая	NCS S 0300-N	4,66	Окраска, Tikkurila, матовая, подготовка Q3	NCS S 0502-Y	23,61	Плинтус МДФ h=69 мм, SX165	NCS S 0300-N	7,9	Инженерная доска, 1167-4250, 2100×127 мм, на клею; тип 1, отм. ЧП +3,230	4,66	Н стен 2900 (до потолка)

Примечания

1. Ведомость продолжена на листе 3 из 3; итоги, сводка площадей и примечания — на последнем листе ведомости.

					Проект: Дом 120 м²
	Лист	№ док.	Подпись	Дата	
Дизайнер	Кырлан А.С.			04.11.26	Ведомость отделки помещений. Лист 2 из 3

Стадия	Лист	Листов
П	С2	136

Ведомость отделки помещений (форма 1 прил. А ГОСТ 21.501-2018). Лист 3 из 3

№	Наименование помещения	Потолок			Стены и перегородки			Низ стен (плинтус)			Пол		Примечание
		Вид отделки	Код цвета	S, м²	Вид отделки	Код цвета	S, м²	Вид отделки	Код цвета	L, м	Вид отделки	S, м²	
10	Холл второго этажа 15,51 м²	ГКЛ по каркасу П113, отм. +6,030; окраска, Little Greene Absolute Matt, глубокоматовая, 2 слоя, подготовка Q3	Little Greene No. 222	15,51	Окраска, Tikkurila, матовая, 2 слоя, подготовка Q3	Tikkurila G503	33,04	Плинтус МДФ h=80 мм, аналог: МДФ под покраску 80×16	Tikkurila G503	11,1	Инженерная доска, 1167-4250, 2100×127 мм, на клею; тип 1, отм. ЧП +3,230	15,51	Н стен 2800 (до потолка); матовая моющаяся, класс 1 EN 13300 — осознанно вместо полуматовой; краска бренда веера G503 — Tikkurila матовая линейка класса 1 — по каталогу Tikkurila при закупке; краска бренда веера Little Greene; класс по EN 13300 и блеск линейки — по ТУ Little Greene, в базе не сверены; плинтус в цвет: стены
11	Коридор второго этажа 5,16 м²	ГКЛ по каркасу П113, отм. +5,980; окраска, Little Greene Absolute Matt, глубокоматовая, 2 слоя, подготовка Q3	Little Greene No. 222	5,16	Окраска, Tikkurila, матовая, 2 слоя, подготовка Q3	Tikkurila G503	17,94	Плинтус МДФ h=80 мм, аналог: МДФ под покраску 80×16	Tikkurila G503	5,7	Инженерная доска, 1167-4250, 2100×127 мм, на клею; тип 1, отм. ЧП +3,230	5,16	Н стен 2750 (до потолка); матовая моющаяся, класс 1 EN 13300 — осознанно вместо полуматовой; краска бренда веера G503 — Tikkurila матовая линейка класса 1 — по каталогу Tikkurila при закупке; краска бренда веера Little Greene; класс по EN 13300 и блеск линейки — по ТУ Little Greene, в базе не сверены; плинтус в цвет: стены
12	Детская вторая 9,23 м²	ГКЛ по каркасу П113, отм. +5,930; +6,030; окраска, Little Greene Absolute Matt, глубокоматовая, 2 слоя, подготовка Q3	Little Greene No. 222	9,23	Окраска, Tikkurila, полуматовая, 2 слоя, подготовка Q3 Акцент — стена А: окраска, Tikkurila, полуматовая, 2 слоя, подготовка Q3	Tikkurila G503 Tikkurila H440	22,32 6,80	Плинтус МДФ h=69 мм, SX165	Tikkurila G503	11,4	Инженерная доска, 1167-4250, 2100×127 мм, на клею; тип 1, отм. ЧП +3,230	9,23	Н стен 2700 (до потолка); краска бренда веера Little Greene; класс по EN 13300 и блеск линейки — по ТУ Little Greene, в базе не сверены; плинтус в цвет: стены
13	Санузел второго этажа 5,31 м²	ГКЛВ по каркасу П113, отм. +5,830; окраска, Little Greene Intelligent Bathroom, матовая, 2 слоя, подготовка Q3	Little Greene No. 222	5,31	Облицовка плиткой, A8UZ, 600×1200×9 мм, клей C2 TE S1, затирка CG2WA	Atlas Concorde A8UZ	19,06	нет			Аналог: керамогранит ректифицированный под травертин, матовый, 600×600×9 мм; тип 2, отм. ЧП +3,215	5,31	Н стен 2615 (до потолка); гидроизоляция обмазочная, 2 слоя, с заведением на стены 200 мм; над ванной — до 2000 и 300 мм за борт (по пирогу пола); тест проливом и акт скрытых работ; краска бренда веера Little Greene класс по EN 13300 и блеск линейки — по ТУ Little Greene, в базе не сверены
	Итого			**147,36**			**395,43**			**131,9**		**147,36**	

Примечания

1. Площади поверхностей — по чистым граням стен до отделки: стены = периметр × высоту от чистого пола помещения до низа потолка минус проёмы (облицовка плиткой — до верха облицовки); плинтус = периметр минус дверные проёмы; пол и потолок — по площади помещения. Количество плиток по раскладке. Площади помещений — с учётом всех частей помещения; откосы в площадь стен не входят.
2. Акцентные стены и фартук — отдельными строками, их площадь вычтена из основной отделки стен помещения; фартук — над нижними модулями кухни от столешницы до низа навесных шкафов, где шкафов нет — на 600 мм.
3. Плинтус — длина по периметру за вычетом дверных проёмов; примыкания к наличникам и встроенной мебели — по развёрткам.
4. Формат плитки — Ш×В×Т (ширина × высота в положении укладки × толщина), мм; на полу — вдоль стен А/В × вдоль стен Б/Г.
5. Коды цвета — по веерам производителей; колеровка каждой краски одной партией, проверка выкраса при свете D65 и при лампах проекта.
6. Уровни подготовки Q1–Q4 — система Knauf, не норма ГОСТ/СП; допуски поверхностей — по СП 71.13330.2017 (действующая редакция).
7. «аналог:» — изделие задано характеристиками, марку и артикул согласовать с заказчиком до закупки.
8. Сводка площадей по материалам, м²: потолок — Little Greene No. 222 Absolute Matt — 133,22; потолок — Little Greene No. 222 Intelligent Bathroom — 9,48; потолок — NCS S 0300-N — 4,66; стены — Tikkurila G503 — 266,47; стены — NCS S 3050-R80B — 10,31; стены — NCS S 5020-G90Y 10,47; стены — облицовка плиткой 600×1200×9 мм, Atlas Concorde A8UZ — 36,46; стены — Farrow & Ball No. 89 Modern Emulsion — 7,21; стены Farrow & Ball No. 66 — 10,10; стены — Little Greene No. 222 Intelligent Matt — 22,06; стены — NCS S 0502-Y — 23,61; стены — Tikkurila H440 6,80; фартук — облицовка керамогранитом 1200×600×9 мм — 1,94.

					Проект: Дом 120 м²
	Лист	№ док.	Подпись	Дата	Ведомость отделки помещений. Лист 3 из 3
Дизайнер	Кырлан А.С.			04.11.26	

Стадия	Лист	Листов
П	С3	136

Поз.	Наименование и техническая характеристика	Тип, марка, обозначение документа	Код продукции	Поставщик	Ед. изм.	Кол.	Образец	Примечание
	Лакокрасочные материалы							
1	Краска интерьерная водно-дисперсионная акриловая для стен, матовая, класс мокрого истирания 1 по EN 13300, база A; цвет по вееру Tikkurila G503 «Calla», колеровка машинная	Tikkurila		Tikkurila	л	59,4		поз. К1 колерной карты; пом. 1, 2, 3, 5, 6, 10, 11; S = 220,1 м² × 2 сл. × 0,12 л/м² = 52,8 л, +10 % и 0,5 л на подкраску → ≥ 58,6 л; тара 6 × 9 л + 2 × 2,7 л
2	Краска интерьерная водно-дисперсионная акриловая для акцентных стен, матовая, класс мокрого истирания 1 по EN 13300, база C; цвет NCS S 3050-R80B «Эгейский синий», колеровка машинная	Tikkurila		Tikkurila	л	3,6		поз. К2 колерной карты; пом. 1; S = 10,3 м² × 2 сл. × 0,12 л/м² = 2,5 л, +10 % и 0,5 л на подкраску → ≥ 3,2 л; тара 1 × 2,7 л + 1 × 0,9 л
3	Краска интерьерная водно-дисперсионная акриловая для потолков, глубокоматовая, класс мокрого истирания 2 по EN 13300, база A; цвет по вееру Little Greene No. 222 «Loft White», колеровка машинная	Little Greene Absolute Matt		Little Greene	л	35,7		поз. К3 колерной карты; пом. 1, 2, 3, 5, 6, 7, 8, 10, 11, 12; S = 133,2 м² × 2 сл. × 0,12 л/м² = 32,0 л, +10 % и 0,5 л на подкраску → ≥ 35,7 л; тара — кратно фасовке продукта
4	Краска интерьерная водно-дисперсионная акриловая для акцентных стен, матовая, класс мокрого истирания 1 по EN 13300, база C; цвет NCS S 5020-G90Y «Олива», колеровка машинная	Tikkurila		Tikkurila	л	3,6		поз. К5 колерной карты; пом. 3; S = 10,5 м² × 2 сл. × 0,12 л/м² = 2,5 л, +10 % и 0,5 л на подкраску → ≥ 3,3 л; тара 1 × 2,7 л + 1 × 0,9 л
5	Краска интерьерная водно-дисперсионная акриловая для потолков, матовая, класс мокрого истирания 1 по EN 13300, база A; цвет по вееру Little Greene No. 222 «Loft White», колеровка машинная	Little Greene Intelligent Bathroom		Little Greene	л	3,1		поз. К6 колерной карты; пом. 4, 13; S = 9,5 м² × 2 сл. × 0,12 л/м² = 2,3 л, +10 % и 0,5 л на подкраску → ≥ 3,0 л; тара — кратно фасовке продукта
6	Краска интерьерная водно-дисперсионная акриловая для акцентных стен, матовая, класс мокрого истирания 1 по EN 13300, база C; цвет по вееру Farrow & Ball No. 89 «Lulworth Blue — светлая морская лазурь», колеровка машинная	Farrow & Ball Modern Emulsion		Farrow & Ball	л	2,5		поз. К7 колерной карты; пом. 6; S = 7,2 м² × 2 сл. × 0,12 л/м² = 1,7 л, +10 % и 0,5 л на подкраску → ≥ 2,4 л; тара 1 × 2,5 л
7	Краска интерьерная водно-дисперсионная акриловая для стен, полуматовая, класс мокрого истирания 1 по EN 13300, база A; цвет по вееру Tikkurila G503 «Calla», колеровка машинная	Tikkurila		Tikkurila	л	13,5		поз. К8 колерной карты; пом. 7, 12; S = 46,3 м² × 2 сл. × 0,12 л/м² = 11,1 л, +10 % и 0,5 л на подкраску → ≥ 12,7 л; тара 1 × 9 л + 1 × 2,7 л + 2 × 0,9 л
8	Краска интерьерная водно-дисперсионная акриловая для акцентных стен, полуматовая, класс мокрого истирания 1 по EN 13300, база C; цвет по вееру Farrow & Ball No. 66 «India Yellow — охра / горчица итальянских фасадов», колеровка машинная	Farrow & Ball		Farrow & Ball	л	5		поз. К9 колерной карты; пом. 7; S = 10,1 м² × 2 сл. × 0,12 л/м² = 2,4 л, +10 % и 0,5 л на подкраску → ≥ 3,2 л; тара 1 × 5 л
9	Краска интерьерная водно-дисперсионная акриловая для стен, матовая, класс мокрого истирания 1 по EN 13300, база A; цвет по вееру Little Greene No. 222 «Loft White», колеровка машинная	Little Greene Intelligent Matt		Little Greene	л	6,4		поз. К11 колерной карты; пом. 8; S = 22,1 м² × 2 сл. × 0,12 л/м² = 5,3 л, +10 % и 0,5 л на подкраску → ≥ 6,3 л; тара — кратно фасовке продукта
10	Краска интерьерная водно-дисперсионная акриловая для стен, матовая, класс мокрого истирания 2 по EN 13300, база A; цвет NCS S 0502-Y, колеровка машинная	Tikkurila		Tikkurila	л	7,2		поз. К13 колерной карты; пом. 9; S = 23,6 м² × 2 сл. × 0,12 л/м² = 5,7 л, +10 % и 0,5 л на подкраску → ≥ 6,7 л; тара 2 × 2,7 л + 2 × 0,9 л
11	Краска интерьерная водно-дисперсионная для потолков, глубокоматовая, класс мокрого истирания 2 по EN 13300, база A; цвет NCS S 0300-N, колеровка машинная	Tikkurila		Tikkurila	л	1,8		поз. К14 колерной карты; пом. 9; S = 4,7 м² × 2 сл. × 0,12 л/м² = 1,1 л, +10 % и 0,5 л на подкраску → ≥ 1,7 л; тара 2 × 0,9 л
12	Краска интерьерная водно-дисперсионная акриловая для акцентных стен, полуматовая, класс мокрого истирания 1 по EN 13300, база C; цвет по вееру Tikkurila H440 «H440 Wave — бирюзово-голубая вода», колеровка машинная	Tikkurila		Tikkurila	л	2,7		поз. К16 колерной карты; пом. 12; S = 6,8 м² × 2 сл. × 0,12 л/м² = 1,6 л, +10 % и 0,5 л на подкраску → ≥ 2,3 л; тара 1 × 2,7 л
13	Краска для МДФ и дерева в цвет Tikkurila G503 «Calla» — окраска плинтуса; блеск не ниже блеска стен	марка не задана			л	2,9		поз. К4, К10; пом. 1, 2, 3, 5, 6, 7, 10, 11, 12; L = 116,5 м, S = 10,9 м² × 2 сл. × 0,12 л/м² + 10 %; продукт подобрать в веере Tikkurila
14	Краска для МДФ и дерева в цвет Little Greene No. 222 «Loft White» — окраска плинтуса; блеск не ниже блеска стен	марка не задана			л	0,5		поз. К12; пом. 8; L = 7,4 м, S = 0,7 м² × 2 сл. × 0,12 л/м² + 10 %; продукт подобрать в веере Little Greene
15	Акрил, полуматовая в цвет NCS S 0300-N — окраска плинтуса	аналог по характеристикам			л	0,5		поз. К15; пом. 9; L = 7,9 м, S = 0,7 м² × 2 сл. × 0,12 л/м² + 10 %; продукт подобрать в веере NCS
16	Грунтовка акриловая под окраску стен и потолков — из системы производителя краски	по системе краски			м²	505		площадь окраски стен, акцентов и потолков; 1 слой перед окраской; расход — по ТУ грунтовки

					Проект: Дом 120 м²
	Лист	№ док.	Подпись	Дата	Спецификация отделочных материалов
Дизайнер	Кырлан А.С.			04.11.26	

Стадия	Лист	Листов
П	С4	136

Поз.	Наименование и техническая характеристика	Тип, марка, обозначение документа	Код продукции	Поставщик	Ед. изм.	Кол.	Образец	Примечание
	Плитка и керамогранит							
17	Керамогранит под травертин, 600×600×9 мм, ректификат, водопоглощение 0,1 % (BIa), противоскольжение R10, PEI IV	аналог по характеристикам			м²	14,04		шов 2 мм; Санузел гостевой, пол; Санузел второго этажа, пол; по раскладке 35 шт (S = 9,48 м²), с запасом 39 шт
18	A8UZ, 600×1200×9 мм, ректификат, водопоглощение 0,1 % (BIa), противоскольжение R10, PEI IV	A8UZ		Atlas Concorde	м²	83,52		шов 2 мм; Санузел гостевой, стены А–Г; Санузел гостевой, короб инсталляции; Санузел второго этажа, стены А–Г; Санузел второго этажа, короб инсталляции; Прихожая, пол; по раскладке 103 шт (S = 50,21 м²), с запасом 116 шт
19	Керамогранит под травертин, матовый, 1200×600×9 мм, ректификат, водопоглощение 0,1 % (BIa)	аналог по характеристикам			м²	6,48		шов 2 мм; Гостиная-кухня, фартук (ст. А); Гостиная-кухня, фартук (ст. Б); по раскладке 7 шт (S = 1,94 м²), с запасом 9 шт
	Напольные покрытия							
20	1167-4250, рабочий слой 4 мм, эмиссия E1, укладка на клей	1167-4250		Coswick	м²	129,5		пом. 1, 2, 3, 6, 7, 8, 10, 11, 12; S = 121,02 м² + 7 % (прямая укладка); к заказу — кратно упаковке
21	1167-4250, класс 33, рабочий слой 4 мм, эмиссия E1, укладка на клей	1167-4250		Coswick	м²	5		пом. 9; S = 4,66 м² + 7 % (прямая укладка); к заказу — кратно упаковке
22	Клей для паркета и инженерной доски, эластичный (СМП / полиуретановый)	по рекомендации производителя доски			м²	126		площадь приклейки; расход и шпатель — по ТУ клея
	Погонажные изделия							
23	Плинтус МДФ под покраску 80×16, крепление к стене, окраска в цвет Tikkurila G503	аналог по характеристикам			м	102		пом. 1, 2, 3, 5, 6, 10, 11; L = 91,9 м (периметр без дверных проёмов) + 10 % на подрезку; в штуках — по длине планки
24	SX165, h = 69 мм, крепление к стене, окраска в цвет Tikkurila G503	SX165		Orac Decor	м	28		пом. 7, 12; L = 24,6 м (периметр без дверных проёмов) + 10 % на подрезку; в штуках — по длине планки
25	Плинтус МДФ под покраску 80×16, крепление к стене, окраска в цвет Little Greene No. 222	аналог по характеристикам			м	9		пом. 8; L = 7,4 м (периметр без дверных проёмов) + 10 % на подрезку; в штуках — по длине планки
26	SX165, h = 69 мм, крепление к стене, окраска в цвет NCS S 0300-N	SX165		Orac Decor	м	9		пом. 9; L = 7,9 м (периметр без дверных проёмов) + 10 % на подрезку; в штуках — по длине планки
	Смеси и материалы для облицовки							
27	Затирка для швов плитки, класс CG2WA по EN 13888	Mapei Ultracolor Plus 132		Mapei	кг	5,2		по раскладке (a+b)/(a·b) × шов × t × 1,6 + 10 %; в т. ч. 1,1 кг — позиции раскладки без марки
28	Клей плиточный C2 TE S1 по EN 12004, слой 5 мм	Ceresit CM 17		Ceresit	кг	516		21 меш. по 25 кг; 1,5 кг/м² на 1 мм слоя + 10 %; в т. ч. 115 кг — позиции раскладки без марки
29	Гидроизоляция обмазочная мокрых зон: пол, стены по периметру, зоны замачивания; 2 слоя с армирующей лентой в углах	аналог по характеристикам			м²	19,6		площадь по листу раскладки плитки + 10 %; расход смеси — по ТУ
30	Лента демпферная по периметру пола из плитки	аналог по характеристикам			м	33,3		периметр без дверных проёмов + 10 %

Примечания

1. Количества — из геометрии проекта: площади поверхностей по чистым граням стен до отделки (те же, что в ведомости отделки и колерной карте), плитка, клей и затирка — по раскладке плиточника; в графе «Кол.» — к заказу, с запасом.
2. Краска: расход 0,12 л/м² на слой в 2 слоя, если по ТУ не задан иной; запас 10 % и 0,5 л на подкраску каждого кода. Один код — одна партия, колеровка машинная в колеровочном центре бренда; в заказ — только после утверждения выкраса (колерная карта). Фасовка — по каталогу бренда на дату выпуска; к заказу — не меньше расчётного объёма.
3. «Аналог по характеристикам» — допускается изделие другого производителя с характеристиками не ниже указанных, по согласованию с автором проекта.
4. Графы «Код продукции» и «Масса 1 ед.» не заполнены: коды по классификатору продукции не присвоены, масса единицы до 25 кг (ГОСТ 21.110-2013).
5. Грунтовка и клей для доски указаны площадью обработки; объём — по ТУ выбранного продукта.

					Проект: Дом 120 м²
	Лист	№ док.	Подпись	Дата	
Дизайнер	Кырлан А.С.			04.11.26	Спецификация отделочных материалов

Стадия	Лист	Листов
П	С5	136

Список покупок: материалы для магазина

№	Что купить	Артикул или характеристика	Нужно с запасом	Брать в магазине	Фасовка	Уточнить в магазине	Помещения	Кто покупает
Покрытия полов и облицовка								
1	Инженерная доска (дуб натуральный, рабочий слой 4 мм, эмиссия E1, прямая укладка)	1167-4250	135,71 м²	135,8 м²		уточнить в магазине: м² в упаковке	1, 2, 3, 6, 7, 8, 9, 10, 11, 12	по проекту
2	Клей для паркетной и инженерной доски (эластичный, по ТУ изготовителя доски)	на выбор бригады по проекту	126,83 м²			уточнить в магазине: расход и фасовку — по выбранному продукту		бригада
3	Керамогранит 600×600 мм под травертин	по характеристике: керамогранит под травертин	39 шт	39 шт		уточнить в магазине: штук в коробке	4, 13	по проекту
4	Керамогранит 600×1200 мм A8UZ	A8UZ	114 шт	116 шт		уточнить в магазине: штук в коробке	4, 5, 13	по проекту
5	Керамогранит 1200×600 мм под травертин, матовый	по характеристике: керамогранит под травертин, матовый	8 шт	9 шт		уточнить в магазине: штук в коробке	1	по проекту
Сухие смеси и гидроизоляция								
6	Клей плиточный цементный класса C2 TE S1 (ГОСТ Р 56387-2018)	Ceresit CM 17 или аналог	515,53 кг	21 меш.	мешок 25 кг			по проекту
7	Затирка цементная класса CG2WA, цвет — по колерной карте	Mapei Ultracolor Plus 132 или аналог	5,18 кг	3 упак.	упак. 2 кг			по проекту
8	Гидроизоляция обмазочная полимерная, 2 слоя, лента в углах, манжеты на выводах	на выбор бригады по проекту	19,6 м²			уточнить в магазине: расход и фасовку — по выбранному продукту	4, 13	бригада
9	Лента демпферная по периметру пола из плитки	на выбор бригады по проекту	33,35 м	34 м		уточнить в магазине: фасовку		бригада
10	Смесь цементно-песчаная для стяжки М200 (50 мм, 33 мм)	на выбор бригады по проекту	7,65 м³			уточнить в магазине: расход и фасовку — по выбранному продукту		бригада
11	Смесь штукатурная гипсовая для машинного и ручного нанесения по маякам, слой до 10 мм	на выбор бригады по проекту	413,08 м²			уточнить в магазине: расход и фасовку — по выбранному продукту	1, 2, 3, 4, 5, 6, 7, 8, 10, 11, 12, 13	бригада
Короба из ГКЛВ								
12	Лист ГКЛВ 12,5 мм, 2500 × 1200 мм, обшивка коробов в 2 слоя	на выбор бригады по проекту	7,11 м²	3 лист.	лист 3,00 м²		4, 13	бригада
13	Профиль стальной оцинкованный 27 × 28 мм: каркас коробов (стойки и направляющие)	на выбор бригады по проекту	17,16 м	6 шт	хлыст 3 м			бригада
Слаботочные сети								
14	Кабель домофона — тип по системе поставщика	на выбор бригады по проекту	6,1 м	7 м		уточнить в магазине: длину бухты		бригада
15	Кабель коаксиальный RG-6 (75 Ом) к розеткам ТВ	на выбор бригады по проекту	16,7 м	17 м		уточнить в магазине: длину бухты		бригада
16	Кабель U/UTP кат. 6 (LAN, Wi-Fi и камеры по PoE)	на выбор бригады по проекту	71 м	71 м		уточнить в магазине: длину бухты		бригада
17	Гофротруба Ø20 для слаботочных линий, отдельно от силовых	на выбор бригады по проекту	84,4 м	85 м		уточнить в магазине: длину бухты		бригада
18	Розетка компьютерная RJ45, кат. 6, с рамкой и подрозетником	на выбор бригады по проекту	4 шт	4 шт	шт			бригада
19	Розетка телевизионная (коаксиальная) с рамкой и подрозетником	на выбор бригады по проекту	1 шт	1 шт	шт			бригада
20	Трубка или монитор домофона (поставка домофонной организации)	на выбор бригады по проекту	1 шт	1 шт	шт			по проекту
21	Щит слаботочный ЩС: корпус, DIN-рейка, розетки 220 В	на выбор бригады по проекту	1 шт	1 шт	шт			бригада
22	Патч-панель, портов не менее 6	на выбор бригады по проекту	1 шт	1 шт	шт			бригада
Лакокрасочные материалы								
23	Краска интерьерная акриловая, матовая, класс истирания 1	Tikkurila S 3050-R80B «Эгейский синий»	2,72 л	2 банк.	банка 2,7 л		1	по проекту

					Проект: Дом 120 м²
	Лист	№ док.	Подпись	Дата	
Дизайнер	Кырлан А.С.			04.11.26	Список покупок

Стадия	Лист	Листов
П	С6	136

Список покупок: материалы для магазина (продолжение)

№	Что купить	Артикул или характеристика	Нужно с запасом	Брать в магазине	Фасовка	Уточнить в магазине	Помещения	Кто покупает
24	Краска интерьерная акриловая, матовая, класс истирания 1	Tikkurila G503 «Calla»	58,11 л	22 банк.	банка 2,7 л		1, 2, 3, 5, 6, 10, 11	по проекту
25	Краска интерьерная акриловая, глубокоматовая, класс истирания 2	Little Greene Absolute Matt No. 222 «Loft White»	35,17 л	35,2 л		уточнить в магазине: объём банки	1, 2, 3, 5, 6, 7, 8, 10, 11, 12	по проекту
26	Краска интерьерная акриловая, матовая, класс истирания 1	Tikkurila S 5020-G90Y «Олива»	2,76 л	2 банк.	банка 2,7 л		3	по проекту
27	Краска интерьерная акриловая, матовая, класс истирания 1	Little Greene Intelligent Bathroom No. 222 «Loft White»	2,51 л	2,6 л		уточнить в магазине: объём банки	4, 13	по проекту
28	Краска интерьерная акриловая, матовая, класс истирания 1	Farrow & Ball Modern Emulsion No. 89 «Lulworth Blue — светлая морская лазурь»	1,9 л	1 банк.	банка 2,5 л		6	по проекту
29	Краска интерьерная акриловая, полуматовая, класс истирания 1	Farrow & Ball No. 66 «India Yellow — охра / горчица итальянских фасадов»	2,66 л	2 банк.	банка 2,5 л		7	по проекту
30	Краска интерьерная акриловая, полуматовая, класс истирания 1	Tikkurila G503 «Calla»	12,23 л	5 банк.	банка 2,7 л		7, 12	по проекту
31	Краска интерьерная акриловая, матовая, класс истирания 1	Little Greene Intelligent Matt No. 222 «Loft White»	5,82 л	5,9 л		уточнить в магазине: объём банки	8	по проекту
32	Краска интерьерная акриловая, матовая, класс истирания 2	Tikkurila S 0502-Y	6,24 л	3 банк.	банка 2,7 л		9	по проекту
33	Краска интерьерная водно-дисперсионная, глубокоматовая, класс истирания 2	Tikkurila S 0300-N	1,23 л	1 банк.	банка 2,7 л		9	по проекту
34	Краска интерьерная акриловая, полуматовая, класс истирания 1	Tikkurila H440 «H440 Wave — бирюзово-голубая вода»	1,79 л	1 банк.	банка 2,7 л		12	по проекту
35	Шпаклёвка финишная полимерная под окраску (стены и потолки, Q3)	на выбор бригады по проекту	554,84 м²			уточнить в магазине: расход и фасовку — по выбранному продукту		бригада
36	Грунтовка акриловая глубокого проникновения, 2 слоя	на выбор бригады по проекту	601,15 м²			уточнить в магазине: расход и фасовку — по выбранному продукту		бригада
Погонажные изделия и потолки								
37	Плинтус напольный МДФ под покраску, h=80 мм, крепление к стене	по характеристике: плинтус МДФ под покраску 80×16	109,25 м.п.	46 шт	хлыст 2,4 м		1, 2, 3, 5, 6, 8, 10, 11	по проекту
38	Плинтус напольный МДФ под покраску, h=69 мм, крепление к стене	SX165	35,79 м.п.	15 шт	хлыст 2,4 м		7, 9, 12	по проекту
39	Потолок подвесной ГКЛ/ГКЛВ по каркасу Knauf П113: листы, профили, подвесы, лента, шпаклёвка швов	Knauf П113	134,88 м²			уточнить в магазине: расход и фасовку — по выбранному продукту		по проекту

Примечания


1. «Нужно с запасом» — расход по чертежам и раскладке плюс запас на подрезку и подкраску; «Брать в магазине» — то же количество в единицах, которыми продают (банки, мешки, упаковки, листы, штуки, литры).
2. «Уточнить в магазине» — фасовки этого товара в проекте нет: спросите у продавца, сколько в упаковке, и возьмите целое число упаковок не меньше «Нужно с запасом».
3. Плитку, доску и краску одного цвета берите одной партией (один калибр и тон на помещение) и сохраните чек и номер партии до конца ремонта.
4. «По характеристике» — артикул не выбран: подойдёт любой товар с этими свойствами, согласуйте его с дизайнером до покупки. «Бригада» материал выбирает и закупает бригада по своей технологии.
5. Помещения: 1 — Гостиная-кухня; 2 — Холл с лестницей; 3 — Кабинет; 4 — Санузел гостевой; 5 — Прихожая; 6 — Спальня родителей; 7 — Детская; 8 Гардеробная; 9 — Кладовая; 10 — Холл второго этажа; 11 — Коридор второго этажа; 12 — Детская вторая; 13 — Санузел второго этажа; «—» — материал для нескольких помещений, расход по месту.

					Проект: Дом 120 м²
	Лист	№ док.	Подпись	Дата	Список покупок (окончание)
Дизайнер	Кырлан А.С.			04.11.26	

Стадия	Лист	Листов
П	С7	136


1 Порог 15 мм: мокрая зона — смежное помещение (М 1:5)

Применение: двери Д-3, Д-8

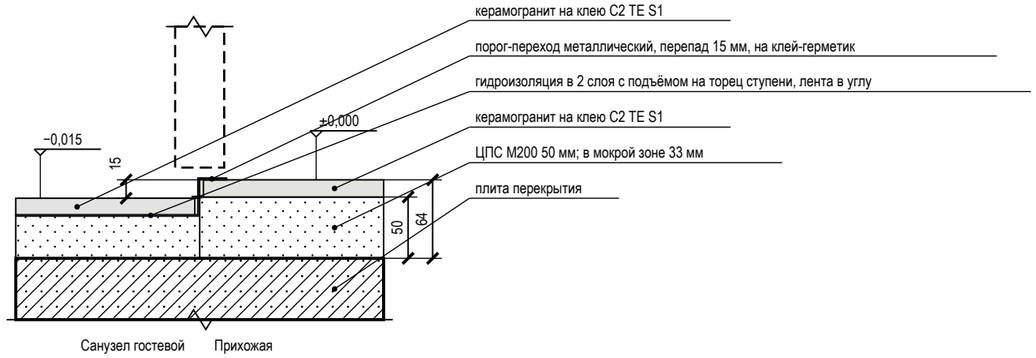


2 Дверь скрытого монтажа в плоскости стены, плинтус (М 1:5)

Применение: двери Д-1, Д-2, Д-3, Д-4, Д-5, Д-6, Д-7, Д-10, Д-9, Д-8

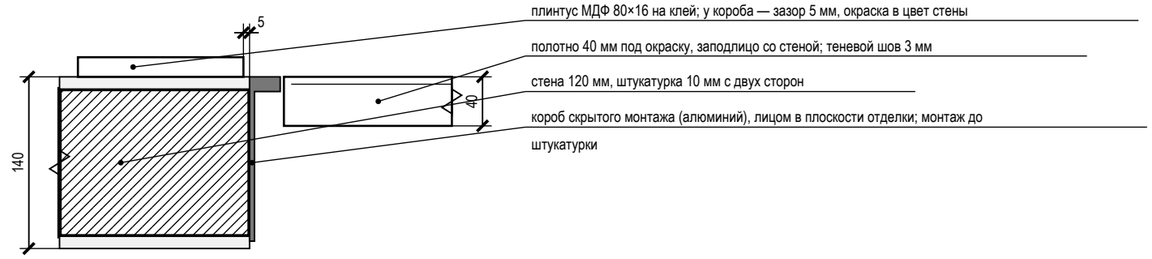


3 Короб стояков К1-1 с люком и звукоизоляцией (М 1:10)

Применение: пом. 4, 1

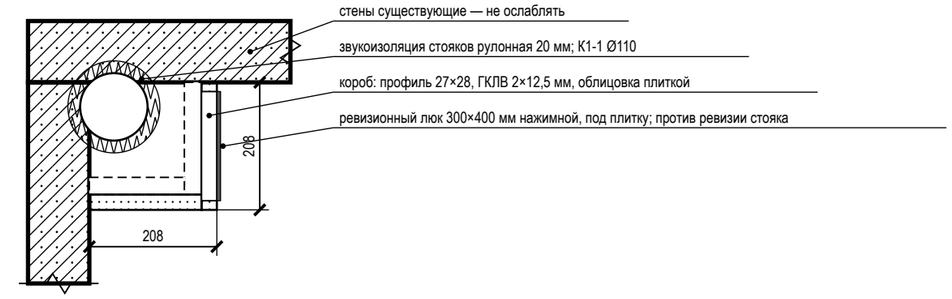


4 Гидроизоляция санузла: заход на стены 200 мм, примыкание ванны (М 1:20)

Применение: пом. 4, 13

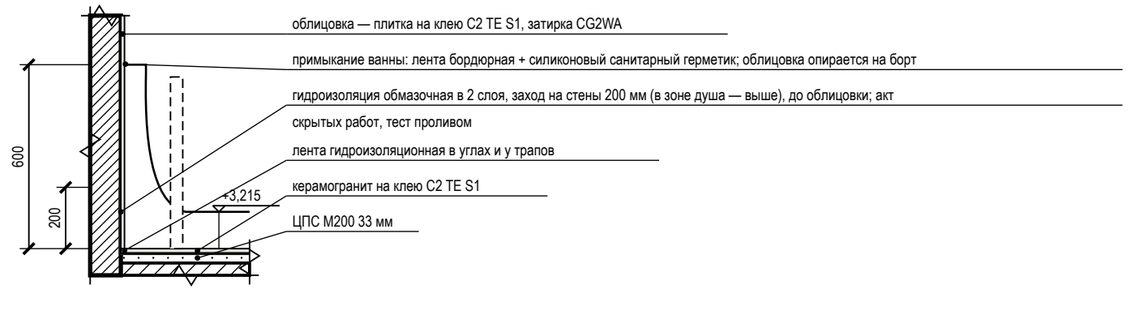


5 Плинтус МДФ 80×16 мм у окрашенной стены по доске (ламинату) (М 1:10)

Применение: пом. 1, 2, 3, 6, 7, 8, 9, 10, 11, 12

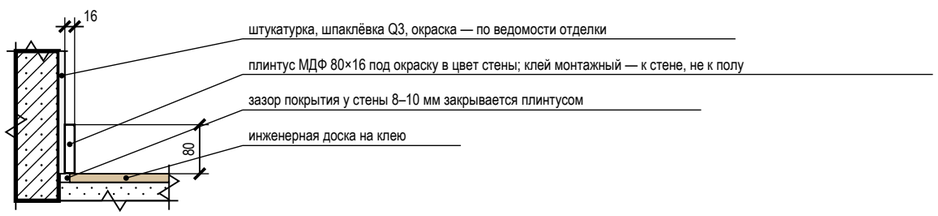

6 Плинтус МДФ 80×16 мм у окрашенной стены по керамограниту (плитке) (М 1:10)

Применение: пом. 5

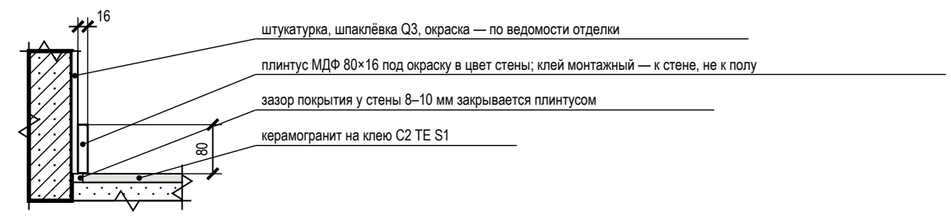

Условные обозначения

- железобетон (плита, стены) — условно: конструкция не установлена
- кладка, перегородка — условно: конструкция не установлена
- стяжка, раствор
- гипсокартон ГКЛВ
- звукоизоляция, эластичный заполнитель
- плитка, керамогранит на клею
- инженерная доска (покрытие пола)
- металлический профиль (порог, Т-профиль, короб двери)
- гидроизоляция (обмазочная, лента)

Примечания

1. Узлы — типовые решения проекта для мест, отмеченных выносками на листе схемы расположения развёрток и узлов; размеры — в мм, отметки — в м от ±0,000 (чистый пол 1-го этажа).
2. Узлы с гидроизоляцией, закладными и коробами скрытого монтажа принимаются по актам скрытых работ до закрытия отделкой; гидроизоляция — после теста проливом (24 ч).
3. Марки изделий (порог, Т-профиль, короб скрытой двери, люк) — по спецификациям; замена — на аналог с теми же габаритами по согласованию с автором проекта.
4. Материал плиты перекрытия и стен в узлах показан условно (железобетон, кладка): конструкция дома не установлена — крепёж, анкеры и толщины слоёв уточняются после обследования (до него — по допущениям общих указаний).
5. Узел 1 применяется на этажах: 1-й этаж, 2-й этаж; отметки показаны для пом. 5 (1-й этаж), на этаже «2-й этаж» — с поправкой +3,230 (разность отметок чистого пола этажей).
6. Узел 4 применяется на этажах: 1-й этаж, 2-й этаж; отметки показаны для пом. 13 (2-й этаж), на этаже «1-й этаж» — с поправкой −3,230 (разность отметок чистого пола этажей).

	Лист	№ док.	Подпись	Дата
Дизайнер	Кырлан А.С.			04.11.26

Проект: Дом 120 м²

Узлы	Стадия	Лист	Листов
	П	С8	136