
L

LINEA

ДИЗАЙН-ПРОЕКТ ИНТЕРЬЕРА

Квартира 68 м², элитный модерн

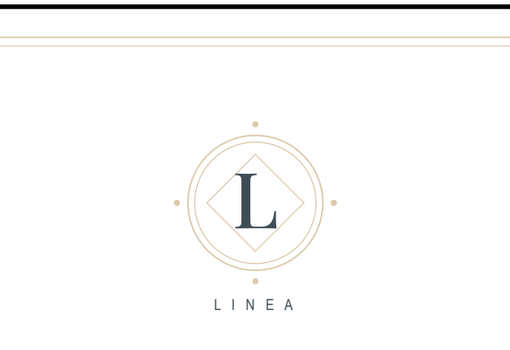

ПАЛИТРА ОТДЕЛКИ

F&B No. 2003	G503	F&B No. 34	F&B No. 281	F&B No. 43
51 %	30 %	6 %	4 %	4 %

АВТОР ПРОЕКТА

Кырлан Александр Сергеевич

Ноябрь 2026

СХЕМАТИЧНАЯ МОДЕЛЬ ПО ПЛАНУ



Построена движком из данных проекта: стены, проёмы, мебель, сантехника, текстиль, декор и цвета отделки — как на листах. Не фотореализм: формы предметов упрощены, свет условный. · ГД-2026-020-АИ · 04.11.2026

Квартира сверху · схематичная модель по плану

ОБЩАЯ ПЛОЩАДЬ	ПОМЕЩЕНИЙ	СТАДИЯ	ШИФР	ОСНОВА
68,47 м²	7, из них жилых 3	Рабочий проект · предварительно	ГД-2026-020-АИ	план заказчика, без обмера

Изм.	Кол.уч	Лист	№ док.	Подп.	Дата
Разраб.		Кырлан А.С.			04.11.26
Пров.					
ГИП					
Н. контр.					
Утв.					

ГД-2026-020-АИ

Квартира 68 м², элитный модерн

Общая площадь 68,47* м² · * размеры приняты, не замерены (реестр — л. 5–7, К-1)

Дизайн-проект интерьера	Стадия	Лист	Листов
	РП	1	105

Титульный лист

М б/м

Кырлан Александр Сергеевич

выпуск 04.11.2026 № 8be4ef4c81 · стр. 1 из 117

Общие данные

ПРЕДВАРИТЕЛЬНО · не для производства работ · открыто пунктов: 25 (реестр — л. 5–7)

Комплект ГД-2026-020-АИ · Квартира · элитный модерн (quiet luxury)

Допущения и предложения на листе. См. лист открытых вопросов (листы 5–7).

Ведомость рабочих чертежей основного комплекта ГД-2026-020-АИ

Лист	Наименование	Примечание
1	Титульный лист	
2	Общие данные	
3	Общие данные	
4	Общие данные	
5	Открытые вопросы, принятые допущения и конфликты. Лист 1 из 3	
6	Открытые вопросы, принятые допущения и конфликты. Лист 2 из 3	
7	Открытые вопросы, принятые допущения и конфликты. Лист 3 из 3	
8	Задание на контрольный обмер и обследование. Лист 1 из 4	
9	Задание на контрольный обмер и обследование. Лист 2 из 4	
10	Задание на контрольный обмер и обследование. Лист 3 из 4	
11	Задание на контрольный обмер и обследование. Лист 4 из 4	
12	График закупок и работ. Лист 1 из 3	
13	График закупок и работ. Лист 2 из 3	
14	График закупок и работ. Лист 3 из 3	
15	Обмерный план	
16	План демонтажа и монтажа перегородок	
17	План дверей и ведомость заполнения проёмов	
18	Концепция интерьера	
19	План расстановки мебели	
20	Спецификация мебели и оборудования	
21	Спецификация мебели и оборудования (продолжение)	
22	Спецификация мебели и оборудования (продолжение)	
23	План розеток и электровыводов	
24	План освещения	
25	План выключателей и схема включения	
26	Ведомость электроточек и изделий	
27	Ведомость электроточек и изделий (продолжение)	
28	Однолинейная схема щита	
29	Однолинейная схема щита (продолжение)	
30	План принципиальных трасс	

Ведомость рабочих чертежей основного комплекта ГД-2026-020-АИ (продолжение)

Лист	Наименование	Примечание
31	План слаботочных сетей	
32	План вентиляции	
33	План отопления	
34	План выводов сантехники	
35	Схема разводки водопровода и канализации	
36	Аксонометрическая схема В1 (холодное водоснабжение)	
37	Аксонометрическая схема Т3 (горячее водоснабжение)	
38	Аксонометрическая схема К1 (канализация)	
39	Развёртки мокрых зон: выводы ВК. Санузел	
40	Развёртки мокрых зон: выводы ВК. Ванная (лист 1 из 2)	
41	Развёртки мокрых зон: выводы ВК. Ванная (лист 2 из 2)	
42	Развёртки мокрых зон: выводы ВК. Кухня-столовая	
43	Спецификация сантехнического оборудования	
44	Техническое задание на подбор светильников	
45	План потолков	
46	Разрезы и узлы потолков	
47	Разрезы и узлы потолков (продолжение)	
48	Сечения потолков М 1:10	
49	Раскладка плитки. Планы полов	
50	Раскладка плитки. Фартук кухни	
51	Раскладка плитки. Санузел. Развёртки стен	
52	Раскладка плитки. Ванная. Развёртки стен	
53	План полов	

Общие указания — лист 4: ±0,000 — чистый пол; несущие конструкции и сети дома — по отдельному проекту; скрытые работы — по актам. Открытые вопросы и допущения — листы 5–7.

Изм.	Кол.уч	Лист	№ док.	Подп.	Дата
Разраб.		Кырлан А.С.			04.11.26
Пров.					
ГИП					
Н. контр.					
Утв.					

ГД-2026-020-АИ

Квартира 68 м², элитный модерн

Общая площадь 68,47* м² · * размеры приняты, не замерены (реестр — л. 5–7, К-1)

Дизайн-проект интерьера

Стадия	Лист	Листов
РП	2	105

Общие данные

М б/м

Кырлан Александр Сергеевич

выпуск 04.11.2026 № 8be4ef4c81 · стр. 2 из 117

Общие данные

Комплект ГД-2026-020-АИ · лист 2 общих данных (продолжение)

Допущения и предложения на листе. См. лист открытых вопросов (листы 5–7).

Ведомость рабочих чертежей основного комплекта ГД-2026-020-АИ (продолжение)

Лист	Наименование	Примечание
54	Ведомость отделки помещений. Лист 1 из 2	
55	Ведомость отделки помещений. Лист 2 из 2	
56	Колерная карта	
57	Спецификация отделочных материалов	
58	Концепция декора и визуализации	
59	План текстиля и декора	
60	Шторы и карнизы	
61	Ведомость текстиля	
62	Ведомость декора. Схемы развески	
63	Схемы развески (продолжение)	
64	Встроенная мебель. Схема расположения	
65	Шкаф-купе М5	
66	Кухня (пом. 5). Развёртка гарнитура	
67	Кухня (пом. 5). Монтажная схема	
68	Шкафы. Монтажная схема	
69	Ведомости изделий, техники и фурнитуры	
70	Реестр марок отделки и позиций альбома	
71	Схема расположения развёрток и узлов	
72	Развёртки стен А, Б. Кабинет (пом. 1)	
73	Привязки электроточек, стена А. Кабинет (пом. 1)	
74	Развёртка стены В. Кабинет (пом. 1)	
75	Развёртка стены Г. Кабинет (пом. 1)	
76	Развёртки стен А, Б, В. Санузел (пом. 2)	
77	Развёртка стены Г. Санузел (пом. 2)	
78	Привязки электроточек и выводов ВК, стена Г. Санузел (пом. 2)	
79	Развёртки стен А, Б. Ванная (пом. 3)	
80	Развёртки стен В, Г. Ванная (пом. 3)	
81	Привязки электроточек и выводов ВК, стена Г. Ванная (пом. 3)	
82	Развёртка стены А. Прихожая (пом. 4)	
83	Развёртки стен Б, В. Прихожая (пом. 4)	

Ведомость рабочих чертежей основного комплекта ГД-2026-020-АИ (продолжение)

Лист	Наименование	Примечание
84	Развёртка стены Г. Прихожая (пом. 4)	
85	Привязки электроточек, стена Г. Прихожая (пом. 4)	
86	Развёртка стены А1. Кухня-столовая (пом. 5), кухонный фронт	
87	Привязки электроточек и выводов ВК, стена А1. Кухня-столовая (пом. 5)	
88	Развёртки стен А2, Б1, Б2. Кухня-столовая (пом. 5)	
89	Развёртки стен В, Г. Кухня-столовая (пом. 5)	
90	Развёртки стен А, Б. Гостиная (пом. 6)	
91	Привязки электроточек, стена А. Гостиная (пом. 6)	
92	Развёртки стен В, Г. Гостиная (пом. 6)	
93	Развёртки стен А1, А2. Спальня (пом. 7)	
94	Развёртка стены Б. Спальня (пом. 7)	
95	Развёртка стены В. Спальня (пом. 7)	
96	Привязки электроточек, стена В. Спальня (пом. 7)	
97	Развёртка стены Г. Спальня (пом. 7)	
98	Узлы	
99	Ведомость объёмов работ	
100	Ведомость объёмов работ (продолжение)	
101	Ведомость объёмов работ (окончание)	
102	Спецификация материалов	
103	Спецификация материалов (окончание)	
104	Смета ориентировочная	
105	Смета ориентировочная (окончание)	

Общие указания — лист 4: ±0,000 — чистый пол; несущие конструкции и сети дома — по отдельному проекту; скрытые работы — по актам. Открытые вопросы и допущения — листы 5–7.

Изм.	Кол.уч	Лист	№ док.	Подп.	Дата
Разраб.		Кырлан А.С.			04.11.26
Пров.					
ГИП					
Н. контр.					
Утв.					

ГД-2026-020-АИ

Квартира 68 м², элитный модерн

Общая площадь 68,47* м² · * размеры приняты, не замерены (реестр — л. 5–7, К-1)

Дизайн-проект интерьера

Стадия	Лист	Листов
РП	3	105

Общие данные

М б/м

Кырлан Александр Сергеевич

выпуск 04.11.2026 № 8be4ef4c81 · стр. 3 из 117

Общие данные

Комплект ГД-2026-020-АИ · лист 3 общих данных (продолжение)

Ведомость ссылочных и прилагаемых документов

Обозначение	Наименование	Примечание
	Ссылочные документы	
ГОСТ 21.201-2011	СПДС. Условные графические изображения элементов зданий, сооружений и конструкций	
ГОСТ 21.205-2016	СПДС. Условные обозначения элементов санитарно-технических систем	
ГОСТ 21.210-2014	СПДС. Изображения условные графические электрооборудования и проводок на планах	
ГОСТ 2.306-68	ЕСКД. Обозначения графические материалов и правила их нанесения на чертежах	
	Прилагаемые документы	
ГД-2026-020-АИ.В1	Визуализация. Вид сверху (3D), схематичная модель по плану: мебель, текстиль и декор из данных проекта	альбом визуализаций

Состав дизайн-проекта

Раздел	Состав	Листы
Обложка	Дизайн-проект интерьера; Квартира 68 м², элитный модерн; автор проекта — Кырлан Александр Сергеевич	1 с.
Концепция	Стиль Современный (контемпорари) 60 % + Тихая роскошь (quiet luxury) 40 %: концепция интерьера, палитра и материалы (колерная карта — лист 56)	л. 18
Визуализации	1 изобр.: Вид сверху (3D), схематичная модель по плану: мебель, текстиль и декор из данных проекта	В1–В1
Рабочие чертежи	планы, развёртки, узлы (развёртки и узлы — листы 39–42, 71, 72, 76, 79, 80, 83, 88–90, 92, 93, 98)	л. 1–105
Спецификации и ведомости	оборудование, изделия, отделка, электроточки	л. 17, 20–22, 26, 27, 43, 54–57, 61, 62, 99–103

4. Нормативные документы, на которые есть ссылки в листах комплекта: ГОСТ Р 21.101-2026; ГОСТ 21.501-2018; ГОСТ 2.302-68; ГОСТ 2.303-68; ГОСТ 2.304-81; ГОСТ 2.307-2011; СП 54.13330.2022; СП 71.13330.2017; СП 73.13330.2016; ПУЭ (7-е изд.), гл. 1.8, 7.1; ГОСТ Р 50571.7.701-2024; СанПиН 1.2.3685-21; ГОСТ 2.702; ГОСТ 2.755; ГОСТ 21.110-2013; ГОСТ 21.601; ГОСТ 475-2016; ГОСТ 23166-2021; ГОСТ 31173-2016; ГОСТ 31565-2012; ГОСТ 32414-2013; ГОСТ 32415-2013; ГОСТ Р 56387-2018; СП 29.13330.2011; СП 30.13330.2020; СП 51.13330.2011; СП 131.13330. Документы из ведомости ссылочных документов здесь не повторяются.
5. За отметку ±0,000 принят уровень чистого пола жилых помещений квартиры (относительная отметка; абсолютная — по проекту дома). Отметка чистого пола мокрых помещений — −0,015. Размеры — в миллиметрах, отметки — в метрах, площади — в м²; высоты установки Н от чистого пола своего помещения до оси изделия.
6. Несущие конструкции, общедомовые стояки, вентиляционные каналы и инженерные сети дома настоящим комплектом не изменяются. Работы, затрагивающие их (проём или штраба в несущей стене, перенос стояка, врезка в вентканал, расширение мокрой зоны), выполняются только по отдельному проекту, к которому прилагается техническое заключение о допустимости и безопасности работ, выданное автором проекта дома или организацией с допуском на обследование, и который согласован в установленном порядке (Жилищный кодекс РФ, ст. 25–29).
7. Трассы инженерных сетей на листах — принципиальные. Расчёты электрических нагрузок и токов КЗ, гидравлики, воздухообмена, освещённости и нагрузок на перекрытие выполняются в проектах ЭОМ, ВК, ОВ и КР организацией с допуском СРО; фактические трассы до закрытия отделкой фиксируются исполнительными схемами.
8. Стиль интерьера — Современный (контемпорари) 60 % + Тихая роскошь (quiet luxury) 40 %. Палитра проекта: основной 60 % Tikkurila G503 «Calla», Farrow & Ball No. 2003 «Pointing», Tikkurila V503 «Winter»; дополнительный 30 % — Farrow & Ball No. 201 «Shaded White», NCS S 2010-Y30R «S 2010-Y30R», Tikkurila H487 «Pumice»; акцент 10 % — NCS S 7010-Y50R «S 7010-Y50R», NCS S 6020-G70Y «S 6020-G70Y», Farrow & Ball No. 298 «Bancha», Farrow & Ball No. 40 «Mouse's Back», Farrow & Ball No. 30 «Hague Blue глубокий сине-зелёный», Farrow & Ball No. 281 «Stiffkey Blue — чернильный синий», Farrow & Ball No. 43 «Eating Room Red брусничный красный», Farrow & Ball No. 34 «Calke Green — традиционный шалфей». Коды цвета — по веерам производителей; цвет утверждается по выкрасу на объекте при освещении проекта.
9. Площади поверхностей — по чистым граням стен до отделки: стены = периметр × высоту от чистого пола помещения до низа потолка минус проёмы (облицовка плиткой — до верха облицовки); плинтус = периметр минус дверные проёмы; пол и потолок — по площади помещения. Количество плиток — по раскладке. Способ один для всех листов комплекта (ведомость отделки, колерная карта, раскладка плитки, развёртки).
10. Марки: стены помещения на всех листах — А (верхняя по плану), Б (правая), В (нижняя), Г (левая); марка отделки О — одна на весь альбом; реестр марок отделки (с позициями колерной карты той же отделки) и марки позиций по видам — на листе 70.
11. Развёртки стен выполнены по всем помещениям для стен с электроточками, мебелью, декором и отделкой: санузлы и кухонный фронт — в М 1:25, остальные стены — в М 1:25; расположение развёрток и узлов — на листе 71, узлы — на листе 98.
12. Перечень скрытых работ, на которые составляются акты освидетельствования (форма по приказу Минстроя России № 344/пр): гидроизоляция пола и стен мокрых помещений (с тестом проливом); стяжка пола (толщина, прочность, влажность основания); тёплый пол до заливки (сопротивление, схема укладки); скрытая электропроводка (за потолком и в штробах стен; условия штробления — в следующем пункте); трубопроводы водоснабжения и канализации до закрытия (опрессовка, уклоны); закладные и усиления под подвесные приборы, мебель и тяжёлый декор, рамы инсталляций; каркасы ГКЛ потолков, коробов и перегородок до обшивки.
13. Скрытая электропроводка: за потолком и в штробах стен. Штробы в стенах выполняются только после технического заключения о несущих конструкциях; до заключения несущие стены не определены, и все стены считаются несущими; объём штроб — в ведомости объёмов работ, строка «Штробы в стенах» (вертикальные спуски; объём не меньше фактического, горизонтальные трассы — по исполнительной схеме).
14. Критерии приёмки: допуски отделочных покрытий — по СП 71.13330.2017; испытания систем водоснабжения и канализации — по СП 73.13330.2016 до закрытия трасс; приёмо-сдаточные испытания электроустановки — по ПУЭ, гл. 1.8, с протоколом электролаборатории.
15. Осознанные отступления от ГОСТ Р 21.101-2026, принятые в комплекте: номер листа и число листов («Листов») указаны на каждом листе; на масштабных листах в основной надписи указан фактический масштаб и дан контрольный отрезок 1000 мм; развёртки стен выполнены в М 1:25 (ГОСТ 21.507-81 — 1:50…1:500) ради читаемости привязок; размерные числа и марки элементов (Д-1, ОК-1, О6) кеглем 2,5 мм, номера помещений — в кружке Ø 8 мм (канон — 3,5 мм и Ø 12 мм): так насыщенные листы А3 читаются без наложений надписей.
16. Графы «Пров.», «Н. контр.», «Утв.» основной надписи заполняются при согласовании комплекта с заказчиком; до согласования комплект подписывает автор проекта (графа «Разраб.»).

Условные обозначения

- контрольный отрезок 1000 мм натуры: по нему проверяют печать 1:1
- отметка уровня, м: ±0,000 — чистый пол жилых помещений
- А — марка развёртки: буква стены, стрелка — взгляд
- О1 — марка отделки по реестру отделки альбома
- выноска узла: над полкой — узел, под полкой — лист

Допущения и предложения на листе

Основа листа: планировка по обводу плана заказчика, не замерена (К-1); высота до плиты 2650 мм от чистого пола — решение автора (ИЗ-1); отметки плана потолков сдвинуты на -95 мм (+2.745 плана = низ плиты), не замерено (К-2); толщины стен приняты: наружные 260 мм, перегородки 130 мм (К-1); положение стен и проёмов — по брифу без обмера и плана БТИ (К-1); разрешённая мощность 10 кВт принята, ТУ не переданы (К-6); вентканалы приняты, в брифе не заданы (К-5); тип дома, перекрытие и несущие стены не известны — документов нет (К-3); плита электрическая — принята, в брифе не указано (К-6); система заземления TN-C-S принята, ТУ не переданы (К-6); число жильцов 2 принято, в брифе не указано (К-9); подрайон климата не задан — принят не северный (жилые от 2,5 м) (К-26).

См. лист открытых вопросов (лист 5, записи К-1, К-3, К-5, К-6, К-9; лист 6, запись К-26).

Общие указания

1. Рабочие чертежи интерьера разработаны на основании задания на проектирование и обмерного плана (лист 15). Объект: Квартира 68 м², элитный модерн; автор проекта — Кырлан Александр Сергеевич; общая площадь 68,47 м², жилая 36,75 м², помещений 7.
2. Рабочие чертежи выполнены в соответствии с заданием на проектирование и нормативными документами, перечисленными в п. 4.
3. Открытые вопросы, принятые допущения и конфликты между разделами, не снятые к выпуску комплекта, сведены в таблицы на листах 5–7. До ответа по пункту таблицы показанное на указанном там листе — допущение, а не утверждённое решение: комплект по этим листам предварительный.

Изм.	Кол.уч	Лист	№ док.	Подп.	Дата
Разраб.		Кырлан А.С.			04.11.26
Пров.					
ГИП					
Н. контр.					
Утв.					

ГД-2026-020-АИ

Квартира 68 м², элитный модерн

Общая площадь 68,47* м² · * размеры приняты, не замерены (реестр — л. 5–7, К-1)

Дизайн-проект интерьера

Стадия	Лист	Листов
РП	4	105

Общие данные

М б/м

Кырлан Александр Сергеевич

выпуск 04.11.2026 № 8be4ef4c81 · стр. 4 из 117

Открытые вопросы, принятые допущения и конфликты. Лист 1 из 3

ПРЕДВАРИТЕЛЬНО · не для производства работ · открыто пунктов: 25 (реестр — л. 5–7)

Сводка по реестрам координации (стартовое совещание 03.11.2026)

Комплект предварительный по пунктам этих таблиц. Пока по пункту нет ответа или решения, показанное на указанном листе — допущение проектировщика, а не утверждённое решение.
Сводка: открытых вопросов — 25 (из них ждут факта объекта — 7: контрольного обмера, обследования или документа); изменений в реестре — 7.
Пункты, ответ на которые лежит на объекте, а не за столом проектировщика (графа «Вид», строка «Ждёт»), собраны на листе «Задание на контрольный обмер и обследование» (листы 8–11): что и где замерить, с какой точностью и чем подтвердить. Пункты, ждущие решения человека, на объекте не закрываются.

Открытые вопросы и принятые допущения

№	Формулировка	Вид	Кто решает	Если решения нет	Лист, где это проявляется
К-1	Планировка принята по обводу плана заказчика, без обмера: план заказчика распознан автоматически по картинке (1 модель ИИ, масштаб — размерные цепочки), затем исправлен исполнителем вручную по размерным числам и рисунку плана (15 правок) и не проверен дизайнером: положение помещений, стен и проёмов — по обводу, контрольный обмер на объекте не выполнялся. От этого зависят все размеры альбома, площади, заказ материалов и изделий. Нужны план БТИ / проект дома и контрольный обмер; до них планировочное решение заменяется обводом плана и уточняется обмером.	Непонятно Ждёт: документа, обмера	Архитектор-планировщик	размеры и расстановка на листах — предложение проектировщика по брифу; мебель на заказ, двери и материалы по ним не заказывать	л. 15 — Обмерный план л. 17 — План дверей и ведомость заполнения проёмов л. 19 — План расстановки мебели
К-3	Тип дома, конструкция перекрытия и несущие стены в брифе не указаны; проект дома, план БТИ и техническое заключение не переданы. До их получения все существующие стены считаются несущими.	Отсутствует Ждёт: документа	Архитектор-планировщик	все существующие стены считаются несущими; демонтаж и штробление в них не выполняются до технического заключения	л. 15 — Обмерный план л. 16 — План демонтажа и монтажа перегородок
К-4	Стояки: на плане потолков есть только знак ∅ в верхнем левом углу ванной (120 мм от стены) — принят за стояк канализации К1 Ø110; стояки В1 и Т3 на плане не показаны и приняты в том же коробе (предложение). Варианты значения знака: стояк / вентканал / вытяжка. Нужен план с инженерией или обмер; от стояков зависят трассы, уклоны и выпуски.	Непонятно Ждёт: обмера	Инженер ВК (вода, канализация)	стояки К1, В1, Т3 в коробе в углу ванной; трассы и уклоны — от них, к монтажу после обмера	л. 34 — План выводов сантехники л. 35 — Схема разводки водопровода и канализации
К-5	Вентканалы в брифе не показаны: приняты у санузла и кухни. От них зависят вытяжка санузла, вытяжка над плитой (до обмера рециркуляция) и короба потолка.	Отсутствует Ждёт: обмера	Инженер ОВ	вытяжка кухни — рециркуляционная; вентилятор санузла по месту канала после обмера	л. 32 — План вентиляции л. 34 — План выводов сантехники
К-6	Разрешённая мощность по ТУ в брифе не указана; принята 10 кВт (квартира с электроплитой). Тип плиты и система заземления в брифе тоже не указаны: приняты электрическая варочная панель и TN-C-S (PE-проводник от ввода) — от них зависят группа плиты, вводной аппарат и защитное заземление. Передать ТУ или справку УК (мощность, система заземления, наличие газа).	Отсутствует Ждёт: документа	Инженер-электрик	щит и группы рассчитаны на 10 кВт, электроплита, TN-C-S; при других ТУ — пересчёт групп варочной панели и духового шкафа, при газе — задание газовику, при TN-C проект заземления	л. 28 — Однолинейная схема щита
К-7	Стиль выбран заказчиком в брифе: Современный (модерн); второй стиль quiet-luxury 40 % — предложение исполнителя (исполнитель, приём заказа 03.11.2026: в рассказе «элитный проект… премиальные материалы» — премиальная составляющая стиля: натуральный камень, широкая доска, шпон, глубокоматовые тёплые нейтрали), не выбор заказчика. Коды палитры подобраны исполнителем по веерам стиля (Современный (контемпорари) + Тихая роскошь (quiet luxury)): стены FarrowBall No. 2003, потолки Tikkurila G503, акценты по комнатам — NCS S 7010-Y50R, NCS S 6020-G70Y, FarrowBall No. 298. Выкрасы не делались. Утвердить стиль и коды по выкрасам.	Спорно Ждёт: решения	Колорист-комплектатор	коды — предложение исполнителя; краску, ткани и фасады не закупать до выкрасов	л. 56 — Колерная карта л. 19 — План расстановки мебели
К-8	Кухня, шкафы и встроенная техника описаны характеристиками («аналог по характеристикам»): модели не выбраны, ниши под технику — по паспорту выбранной модели. Выбрать технику и утвердить проект кухни.	Спорно Ждёт: решения	Мебельщик	выводы кухонной техники — после утверждения проекта кухни; мебель на заказ не заказывать	л. 64 — Встроенная мебель. Схема расположения л. 23 — План розеток и электровыводов
К-9	Состав семьи в брифе не указан (answers.household пуст): принято 2 человека. От числа жильцов зависят обеденная группа, хранение, нагрузка на санузлы и расчётная мощность. Уточнить у заказчика.	Отсутствует Ждёт: решения	Дизайнер интерьера	расстановка и расчёты — на 2 человека	л. 19 — План расстановки мебели л. 28 — Однолинейная схема щита
К-10	Заказчик указал в брифе, что плана нет и нужен обмер: все размеры альбома до обмера — допущение.	Отсутствует Ждёт: обмера	Архитектор-планировщик	альбом не выдаётся к работам до обмера	л. 15 — Обмерный план
К-14	Эркер кухни обмерен частично: окно 1300 мм, глубина ≈ 570 мм, скос к нижней стене ≈ 45° (на листе не обмерен, по рисунку ≈ 1150 мм, вероятно, тоже остеклён). В альбоме эркер приведён к прямоугольнику ступенькой (площадь сохранена ±0,15 м²), окно на скосе не показано. Нужен обмер эркера: длины граней, углы, окна.	Непонятно Ждёт: решения	Архитектор-планировщик	эркер — ступенькой, окно только на прямой грани; ниша штор по эркеру — по плану потолков (250 мм)	л. 15 — Обмерный план
К-15	В верхней (наружной?) стене кухни на плане два узких разрыва ≈ 130 мм (над лентой 13) с участком стены 650 мм между ними. Это вентканалы, окно или проходы коммуникаций — по плану потолков не понять. В альбоме не показаны.	Непонятно Ждёт: решения	Архитектор-планировщик	не учитываются; кухонный гарнитур вдоль верхней стены до проверки на месте	л. 15 — Обмерный план
К-16	Входная дверь на плане не помечена (марки Д-1…Д-5 — межкомнатные). Принят вход через проём 880 мм в нижней стене прихожей (единственный разрыв наружной стены без окна).	Непонятно Ждёт: решения	Архитектор-планировщик	вход — там; входной блок — по замеру проёма	л. 15 — Обмерный план

Изм.	Кол.уч	Лист	№ док.	Подп.	Дата
Разраб.		Кырлан А.С.			04.11.26
Пров.					
ГИП					
Н. контр.					
Утв.					

ГД-2026-020-АИ

Квартира 68 м², элитный модерн

Общая площадь 68,47* м² · * размеры приняты, не замерены (реестр — л. 5–7, К-1)

Дизайн-проект интерьера

Стадия	Лист	Листов
РП	5	105

Открытые вопросы, принятые допущения и конфликты. Лист 1 из 3
М б/м

Кырлан Александр Сергеевич

выпуск 04.11.2026 № 8be4ef4c81 · стр. 5 из 117

Открытые вопросы, принятые допущения и конфликты. Лист 2 из 3

Сводка по реестрам координации (стартовое совещание 03.11.2026)

Открытые вопросы и принятые допущения (продолжение)

№	Формулировка	Вид	Кто решает	Если решения нет	Лист, где это проявляется
К-17	Проём из прихожей в спальню (880 мм) без марки Д — это проём без двери или дверь, не попавшая в ведомость Д? Варианты: (1) дверь 800 с полотном, как остальные; (2) открытый проём. Рекомендация — (1): спальня не проходная.	Непонятно Ждёт: решения	Архитектор-планировщик	дверь 800 × 2100 с полотном, открывание в спальню	л. 15 — Обмерный план
К-18	В правом верхнем углу спальни прямоугольник ≈ 1300 × 290 мм вне контура потолка (без подписи): короб, шахта, пилон или шкаф. В альбоме — вне помещения.	Непонятно Ждёт: решения	Архитектор-планировщик	участок вне помещения, мебель к нему не ставится	л. 15 — Обмерный план
К-19	У левой стены кухни рядом с Д-4 на плане синий участок «залізобетон» ≈ 640 × 90 мм (выступ стены, ригель или колонна?). В альбоме не показан.	Непонятно Ждёт: решения	Архитектор-планировщик	не учитывается до обмера	л. 15 — Обмерный план
К-20	Светильники перенесены с исходного плана: марки 01-А, 01-Б, 02, 03, 04, 05, 06-А, 06-Б, 08-А, 08-Б, 09, 10, 12 (бра), 13 (подсветка рабочей поверхности), 13-А, 13-Б, 14 и вентиляторы 11 — место по плану (±30 мм по рисунку), но ведомости светильников нет: тип, мощность, световой поток, цвет света не заданы. Приняты: точечные LED 7 Вт 3000 K Ra ≥ 90; 13-А/13-Б — подвесные у кровати; 12 — настенное бра h 1200 (высота не задана); 09 в чёрной нише — трековые/точечные. Марка 13 на плане двойная: «13 підсвітка роб. пов.» в кухне и «13-А/13-Б» в спальне. Нужны ведомость светильников и схема включения (группы А/Б?).	Непонятно Ждёт: решения	Инженер-электрик	светильники по марке плана с параметрами-допущениями; закупать только после ведомости	л. 24 — План освещения
К-21	Ниша в прихожей «покрасить в чорний (темно-сірий)» — кода цвета нет. Предложение: RAL 7016 (антрацит, из палитры стиля), глубокоматовая. Варианты: RAL 9005 (чёрный) / RAL 7016 / NCS S 8500-N. Потолки по плану — RAL 9010.	Непонятно Ждёт: решения	Колорист-комплектатор	RAL 7016 глубокоматовая; выкрас до покраски	л. 56 — Колерная карта
К-22	Сверка с ведомостью отделки потолка заказчика: по альбому ГКЛ 61,14 м² (в ведомости 60,14), ГКЛ влагостойкий 5,81 (3,83 санузел + ванная по размерам больше), шпаклёвка по ж/б 1,52 (4,08 — ниши по размерам меньше), всего 68,47 (68,05). Возможно, в ведомости санузел или его часть посчитан «по ж/б», а ниша штор эркера — со скосом. Какая ведомость верна — по обмеру; ведомость заказчика не подгоняется.	Спорно Ждёт: решения	Гипсокартонщик	объёмы — по чертежу альбома; перед закупкой — по обмеру	л. 45 — План потолков
К-23	Бюджет в брифе не указан («элитный проект, премиальные материалы» — уровень, не сумма). Смета посчитана по премиальным позициям стиля без потолка суммы.	Отсутствует Ждёт: решения	Сметчик	материалы премиум-уровня стиля; сумма — для согласования, не обязательство	л. 104 — Смета ориентировочная
К-24	Расчётная нагрузка 10,8 кВт (по коэффициентам спроса, без подгонки) больше принятой разрешённой 10 кВт (К-6; ТУ не переданы). Предложение: запросить у сетевой организации / УК увеличение выделенной мощности до 15 кВт — иначе электроплита, тёплый пол и кондиционеры одновременно не работают; либо снять часть нагрузки (тёплый пол, кондиционеры — они предложены по умолчанию).	Спорно Ждёт: решения	Инженер-электрик	щит собран на 10 кВт, расчётная выше разрешённой; тёплый пол и кондиционеры — предложения, к монтажу не принимать до ответа по мощности	л. 28 — Однолинейная схема щита
К-25	Узел ввода воды принят по умолчанию (предложение): на ХВС и ГВС — кран → фильтр грубой очистки → счётчик → обратный клапан → редуктор давления → кран с электроприводом (защита от протечек) → коллектор на 13 выходов; разводка — коллекторная, в стяжке пола, отдельной трубой к каждому прибору, без соединений в полу. Не известны: место узла и коллектора, давление на вводе, Ду вводов, наличие счётчиков и разрешённый способ учёта (УК) — положение стояков принято без обмера (К-4). Нужны обмер, справка УК и решение по составу узла.	Отсутствует Ждёт: решения	Инженер ВК (вода, канализация)	узел ввода, коллектор и электрокраны — предложение, место на листах условное; трубы и арматуру не закупать, штробы и закладные в стяжке не делать до обмера и решения	л. 35 — Схема разводки водопровода и канализации л. 34 — План выводов сантехники
К-26	Климатический подрайон (СП 131.13330) не задан: принят не северный — жилые комнаты и кухня под потолком от 2,5 м (СП 54, п. 5.12); в IA, IБ, IГ, IД, IVA — от 2,7 м.	Отсутствует Ждёт: документа	Архитектор-планировщик	отметки потолков жилых — по 2,5 м; при северном подрайоне уровни ниже 2,7 м пересчитать до заказа каркаса	л. 45 — План потолков
К-27	Унитаз подвесной П4 (пом. 2 «Санузел»), выпуск К1-1 Ø110: выпуск Ø110 на высоте 220 мм в инсталляции; трасса до Ст К1-1 задана «в полу», а в пол она не помещается (нужно 210 мм при пироге 90 мм). Рекомендация исполнителя — короб 170×140 над чистым полом вдоль стен до Ст К1-1 (1,26 м): плитка обходит короб, у двери короб не проходит; это штатная прокладка для подвесного прибора: отвод идёт за инсталляцией и в коробе, пол не поднимается. Варианты: (а) короб 170×140 над чистым полом вдоль стен до Ст К1-1 (1,26 м): плитка обходит короб, у двери короб не проходит; (б) подиум или подъём пола на 120 мм — ступень и порог у входа, высота двери в свету и выводов прибора меняются, пересчёт раскладки плитки; (в) прибор ближе к стояку Ст К1-1 — меняется планировка санузла (расстановка, выводы, раскладка); (г) насосная установка (КНС) у прибора — шум, обслуживание, электропитание, согласование; только если другие варианты невозможны. Решение меняет санузел (высоты, раскладку плитки) — за автором с заказчиком.	Спорно Ждёт: решения	Инженер ВК (вода, канализация)	выпуск К1-1 и прибор П4 не выполнять до решения; остальное — по листам	л. 35 — Схема разводки водопровода и канализации л. 34 — План выводов сантехники

Изм.	Кол.уч	Лист	№ док.	Подп.	Дата
Разраб.		Кырлан А.С.			04.11.26
Пров.					
ГИП					
Н. контр.					
Утв.					

ГД-2026-020-АИ

Квартира 68 м², элитный модерн

Общая площадь 68,47* м² · * размеры приняты, не замерены (реестр — л. 5–7, К-1)

Дизайн-проект интерьера

Стадия	Лист	Листов
РП	6	105

Открытые вопросы, принятые допущения и конфликты. Лист 2 из 3

М б/м

Кырлан Александр Сергеевич

выпуск 04.11.2026 № 8be4ef4c81 · стр. 6 из 117

Открытые вопросы, принятые допущения и конфликты. Лист 3 из 3

Сводка по реестрам координации (стартовое совещание 03.11.2026)

Открытые вопросы и принятые допущения (продолжение)

№	Формулировка	Вид	Кто решает	Если решения нет	Лист, где это проявляется
К-28	Ванна П9 (пом. 3 «Ванная»), выпуск К1-3 Ø50: в полу не помещается: врезка + перепад 62 (2,06 м × 30 мм/м) + Ø50 + слой над трубой 45 = 187 мм при пироге 90 мм. Рекомендация исполнителя — короб 150×110 над чистым полом вдоль стен до Ст К1-1 (2,06 м): плитка обходит короб, у двери короб не проходит; сифон и выпуск прибора — над полом за экраном/корпусом. Варианты: (а) короб 150×110 над чистым полом вдоль стен до Ст К1-1 (2,06 м): плитка обходит короб, у двери короб не проходит; (б) подиум или подъём пола на 100 мм — ступень и порог у входа, высота двери в свету и выводов прибора меняются, пересчёт раскладки плитки; (в) прибор ближе к стояку Ст К1-1 — меняется планировка санузла (расстановка, выводы, раскладка); (г) насосная установка (КНС) у прибора — шум, обслуживание, электропитание, согласование; только если другие варианты невозможны. Решение меняет санузел (высоты, раскладку плитки) — за автором с заказчиком.	Спорно Ждёт: решения	Инженер ВК (вода, канализация)	выпуск К1-3 и прибор П9 не выполнять до решения; остальное — по листам	л. 35 — Схема разводки водопровода и канализации л. 34 — План выводов сантехники
К-29	Циркуляция ГВС в данных не задана — циркуляционного трубопровода на схеме нет. Решить: нужна ли циркуляция	Отсутствует Ждёт: решения	Инженер ВК (вода, канализация)	циркуляции на схеме нет	л. 39–42 — Развёртки мокрых зон: выводы ВК. Санузел л. 36 — Аксонометрическая схема В1 (холодное водоснабжение) л. 35 — Схема разводки водопровода и канализации

Изменения проекта после выпуска листов (реестр изменений)

№	Дата	Лист	Было	Стало	Кто решил, подпись
ИЗ-1	03.11.2026	л. 15 — Обмерный план л. 45 — План потолков	Высота до плиты 2745 мм — по отметке +2.745 плана потолков (К-2).	Решение автора: от чистого пола до плиты 2650 мм; отметки плана −95 мм, перепады сохранены: по плите +2.650, комнаты +2.590, прихожая +2.550, санузел и ванная +2.505. Датум отметок плана — допущение (отдельный вопрос).	Утверждено: Кырлан А.С., 03.11.2026. Предложил: Александр Кырлан, решение автора.
ИЗ-2	03.11.2026	л. 19 — План расстановки мебели	Назначение помещений не подписано (К-11).	Решение автора — по предложению исполнителя: кабинет у окна (бра 12), кухня-столовая с эркером (подсветка 13), гостиная, спальня (подвесы 13-А/13-Б, кровать 1800 между ними).	Утверждено: Кырлан А.С., 03.11.2026. Предложил: Александр Кырлан, решение автора.
ИЗ-3	03.11.2026	л. 34 — План выводов сантехники л. 49 — Раскладка плитки. Планы полов	Ванная и санузел не подписаны (К-12).	Решение автора: большее — ванная (ванна 1700 у правой стены, умывальник на тумбе 800, стиральная машина 600 × 600 с выводами и розеткой на своей группе); меньшее — санузел (подвесной унитаз, гигиенический душ, раковина 400).	Утверждено: Кырлан А.С., 03.11.2026. Предложил: Александр Кырлан, решение автора.
ИЗ-4	03.11.2026	л. 16 — План демонтажа и монтажа перегородок	Несущие стены не известны (К-13).	Решение автора: все существующие стены — несущие до техзаключения; демонтаж и штробление — после него.	Утверждено: Кырлан А.С., 03.11.2026. Предложил: Александр Кырлан, решение автора.
ИЗ-5	03.11.2026	л. 24 — План освещения л. 45 — План потолков	Споты 70 мм в 60 мм запотолочного (К-31).	Решение: встраиваемые светильники тонкие, монтажная глубина ≤ 50 мм; марки исходного плана сохранены; тип — в спецификации с пометкой «глубина ≤ 50 мм».	Утверждено: Кырлан А.С., 03.11.2026. Предложил: Александр Кырлан, решение автора.
ИЗ-6	03.11.2026	л. 32 — План вентиляции	Вентилятор 11 в потолке мокрых: 145 < 150 мм (К-32).	Решение: вытяжная решётка на стене санузла и ванной в канал, вентилятор канальный настенный с обратным клапаном; знак 11 плана — не в потолке.	Утверждено: Кырлан А.С., 03.11.2026. Предложил: Александр Кырлан, решение автора.
ИЗ-7	03.11.2026	л. 15 — Обмерный план	Датум отметок плана не известен (К-30).	Решение: допущение сохраняется — отметки дизайнера на 95 мм ниже чистого пола; подтвердить на обмере (не блокирует выпуск).	Утверждено: Кырлан А.С., 03.11.2026. Предложил: Александр Кырлан, решение автора.

Примечания

1. Номера листов — по ведомости рабочих чертежей комплекта (лист «Общие данные»).
2. Графа «Если решения нет» показывает состояние решения на листах; влияние на сроки и стоимость по пунктам не оценивалось.
3. Пункт, по которому принято решение, при следующем выпуске комплекта из таблиц исключается.

Изм.	Кол.уч	Лист	№ док.	Подп.	Дата			
Разраб.		Кырлан А.С.			04.11.26	ГД-2026-020-АИ		
Пров.						Квартира 68 м², элитный модерн Общая площадь 68,47* м² · * размеры приняты, не замерены (реестр — л. 5–7, К-1)		
ГИП						Дизайн-проект интерьера	Стадия: РП; Лист: 7; Листов: 105	
Н. контр.						**Открытые вопросы, принятые допущения и конфликты. Лист 3 из 3** М б/м	**Кырлан Александр Сергеевич**	
Утв.								

Задание на контрольный обмер и обследование. Лист 1 из 4

ПРЕДВАРИТЕЛЬНО · не для производства работ · открыто пунктов: 25 (реестр — л. 5–7)

Что замерить, вскрыть и получить до заказа материалов и изделий

Задание собрано из открытых вопросов, ответ на которые лежит на объекте или в документах, а не за столом проектировщика. Пока факт не получен, размер, материал или положение на листах — допущение (знак «*»), а не замер.
Сводка: на объекте — 20 (до демонтажа — 18; после демонтажа — 2); документом и при закупке — 4; из допущений в данных и на листах — 21, из них без вопроса в реестре — 4. Закрываются вопросы: К-1, К-3–К-6, К-9, К-10, К-26 (8). Вопросы, ждущие решения человека, задание не закрывает — они решаются по реестру открытых вопросов.

Условия проведения

Порядок работ	Приёмы и точность	Кто присутствует	Если факт не совпал с проектом
1. До демонтажа — существующее состояние: контур, диагонали, высоты, проёмы, оси стояков, ниши и конструкции, которые видны. 2. После демонтажа, до черновых работ — то, что закрывали отделка и короба: основание стен, фактические толщины, углы, узлы. 3. Документы и данные закупки — не на объекте: к сроку из последней таблицы, от них зависят привязки и заказ. Что заказывается по размеру из задания, до закрытия пункта не заказывают: сроки изготовления — по графику закупок прораба.	Обход по часовой стрелке от входа: стены, проёмы, потолок, коммуникации (стояки, щиток, вентканалы), особенности (ниши, короба, выступы). Размеры записывают в мм; сумма участков равна общему размеру, при цепочке длиннее трёх участков ставят проверочный (общий) размер. Диагонали каждого помещения; если две диагонали различаются на 5 мм и больше, разницу подписывают на плане. Потолок — в нескольких точках: центр, углы, у проёмов. Проём — ширина, высота, глубина откоса, привязка к ближайшим углам, высота подоконника. Допустимая погрешность прибора — 2–3 мм на метр; размеры округляют кратно 5 мм; два контрольных промера одного размера не должны расходиться более чем на 2 %. Допуск по пункту — в графе «Точность». План БТИ обмер не заменяет.	Прораб (отвечает за проведение) — назначает день и порядок обхода, открывает объект и освобождает помещения, ведёт это задание и реестр изменений. Архитектор — выполняет обмер, составляет акт контрольного обмера и подписывает результаты по размерам и конструкциям. Владельцы вопросов присутствуют при пунктах своего раздела или принимают результат до заказа: Инженер ВК (вода, канализация) — К-4; Инженер ОВ — К-5; позиции О-2; Инженер-электрик — К-6; позиции О-1; Дизайнер интерьера — К-9; Отделочник — позиции О-19, О-20. Заказчик или его представитель — передаёт документы (план БТИ, проект дома, технические условия, паспорта), подписывает акт. Проектных решений на обмере не принимают: обмер даёт факт, решения — по реестру открытых вопросов (листы 5–7).	1. В пределах допуска пункта — принимается измеренное значение, лист перевыпускается, знак «*» снимается. 2. Больше допуска или контрольные промеры расходятся более чем на 2 % — промер повторяют; не подтвердилось — запись в реестр изменений (дата, лист, было, стало, кто решил, подпись), работы в этом месте не начинают. 3. Затронуты несущая стена, стояк, вентканал или мокрая зона — сразу владельцу раздела и ГИПу (главному инженеру проекта); между разделами не больше двух кругов, затем решает ГИП. 4. На объекте устно ничего не согласуется: каждое решение — записью в реестр с подписью.

Этап 1. До демонтажа

№	Где	Способ	Что сделать	Кто выполняет	Точность	Что пересчитается в альбоме	Чем подтверждается	Закрывает вопросы реестра
О-1	Вход в квартиру или лестничная клетка; место щита на плане	Обмер	Существующий щиток и счётчик электроэнергии: место и габарит ниши, состояние ввода, марка и сечение вводного кабеля, наличие вводного автомата и УЗО, пломбы.	Архитектор	±5 мм	Ниша и место щита на листах; вводной кабель и аппараты на однолинейной схеме; расстояния до первых групп. Листы: л. 28, 29 — Однолинейная схема щита	акт контрольного обмера; фото с рулеткой и привязкой к стене или углу	Вопроса в реестре нет: Альбом принимает щит и ввод без осмотра. Результат принимает: Инженер-электрик
О-2	у окон	Обмер	Положение стояков отопления (подающий и обратный) от граней стен, диаметры, наличие запорной арматуры; существующие радиаторы: число секций, межосевое расстояние, подводки. В данных стояков отопления нет — лист отопления выводит их условно у откоса окна.	Архитектор	±5 мм	План отопления: места стояков и подводок, привязки радиаторов; подбор радиаторов по теплотехническому расчёту; радиаторы и узлы подключения в ВОР и спецификации. Листы: л. 33 — План отопления	акт контрольного обмера; фото с рулеткой и привязкой к стене или углу	Вопроса в реестре нет: Альбом принимает положение стояков и радиаторов отопления без обмера. Результат принимает: Инженер ОВ
О-3	все помещения, обход по часовой стрелке от входа	Обмер	Контрольный обмер всех помещений: чистые размеры, диагонали, толщины стен (приняты наружные 260 мм, внутренние 130 мм), проёмы дверей и окон, подоконники, высота потолка.	исполнитель	±5 мм; диагонали — разница от 5 мм подписывается	все размеры альбома; размеры, по которым заказываются материалы и изделия Листы: л. 15 — Обмерный план л. 17 — План дверей и ведомость заполнения проёмов л. 19 — План расстановки мебели	акт контрольного обмера	К-1 Результат принимает: Архитектор
О-4	По месту	Обмер	Подтвердить на объекте принятое: положение стен и проёмов — по брифу без обмера и плана БТИ	Архитектор	±5 мм	Листы, где используется принятая величина. Листы: л. 2–4 — Общие данные	акт контрольного обмера	К-1 Результат принимает: Архитектор

Допущения и предложения на листе

Основа листа: планировка по обводу плана заказчика, не замерена (К-1); высота до плиты 2650 мм от чистого пола — решение автора (ИЗ-1); отметки плана потолков сдвинуты на -95 мм (+2.745 плана = низ плиты), не замерено (К-2); толщины стен приняты: наружные 260 мм, перегородки 130 мм (К-1); положение стен и проёмов — по брифу без обмера и плана БТИ (К-1); разрешённая мощность 10 кВт принята, ТУ не переданы (К-6); вентканалы приняты, в брифе не заданы (К-5); тип дома, перекрытие и несущие стены не известны — документов нет (К-3); плита электрическая — принята, в брифе не указано (К-6); система заземления TN-C-S принята, ТУ не переданы (К-6); число жильцов 2 принято, в брифе не указано (К-9); подрайон климата не задан — принят не северный (жилые от 2,5 м) (К-26).
См. лист открытых вопросов (лист 5, записи К-1, К-3, К-5, К-6, К-9; лист 6, запись К-26).

Изм.	Кол.уч	Лист	№ док.	Подп.	Дата
Разраб.		Кырлан А.С.			04.11.26
Пров.					
ГИП					
Н. контр.					
Утв.					

ГД-2026-020-АИ

Квартира 68 м², элитный модерн

Общая площадь 68,47* м² · * размеры приняты, не замерены (реестр — л. 5–7, К-1)

Дизайн-проект интерьера

Стадия	Лист	Листов
РП	8	105

Задание на контрольный обмер и обследование.
Лист 1 из 4
М б/м

Кырлан Александр Сергеевич

выпуск 04.11.2026 № 8be4ef4c81 · стр. 8 из 117

Задание на контрольный обмер и обследование. Лист 2 из 4

Что замерить, вскрыть и получить до заказа материалов и изделий

Этап 1. До демонтажа (продолжение)

№	Где	Способ	Что сделать	Кто выполняет	Точность	Что пересчитается в альбоме	Чем подтверждается	Закрывает вопросы реестра
О-5	Ванная (пом. 3): Ст К1-1*, Ст В1-2*, Ст Т3-3; наличие стояка ГВС, арматуры и счётчиков — по всей квартире	Обмер	Положение стояков Ст К1-1*, Ст В1-2*, Ст Т3-3*: привязка осей от граней стен, диаметры, размеры короба и люков. Стояк горячей воды Т3 в данных не задан, на листах ВК принят рядом с стояком холодной воды: выяснить, есть ли он в доме, и где. Отключающая арматура и счётчики воды на вводах: положение, тип, пломбы управляющей компании. Сверить до разметки выводов.	исполнитель	±5 мм	Привязки выводов воды и канализации на планах выводов и разводки; расстояние розеток до стояка; места люков 300 × 400 мм; трассы Т3 и полотенцесушители (водяной или электрический); узлы ввода в спецификации ВК (краны, фильтры, счётчики). трассы В1, Т3, К1, выводы, уклоны, короба Листы: л. 34 — План выводов сантехники л. 35 — Схема разводки водопровода и канализации	акт контрольного обмера; фото с рулеткой и привязкой к стене или углу	К-4 Результат принимает: Инженер ВК (вода, канализация)
О-6	По месту	Обмер	Подтвердить на объекте принятое: вентканалы приняты, в брифе не заданы	Архитектор	±5 мм	Листы, где используется принятая величина. Листы: л. 2–4 — Общие данные	акт контрольного обмера	К-5 Результат принимает: Инженер ОВ
О-7	санузлы, кухня	Обмер	Положение и сечение вентканалов, тяга.	исполнитель	±5 мм	план вентиляции, потолки, вытяжка кухни Листы: л. 32 — План вентиляции л. 34 — План выводов сантехники	акт контрольного обмера; фото с рулеткой и привязкой к стене или углу	К-5 Результат принимает: Инженер ОВ
О-8	По месту	Обмер	Подтвердить на объекте принятое: система заземления TN-C-S принята, ТУ не переданы	Архитектор	±5 мм	Листы, где используется принятая величина. Листы: л. 2–4 — Общие данные	акт контрольного обмера	К-6 Результат принимает: Инженер-электрик
О-9	По месту	Обмер	Подтвердить на объекте принятое: плита электрическая принята, в брифе не указано	Архитектор	±5 мм	Листы, где используется принятая величина. Листы: л. 2–4 — Общие данные	акт контрольного обмера	К-6 Результат принимает: Инженер-электрик
О-10	По месту	Обмер	Подтвердить на объекте принятое: число жильцов 2 принято, в брифе не указано	Архитектор	±5 мм	Листы, где используется принятая величина. Листы: л. 2–4 — Общие данные	акт контрольного обмера	К-9 Результат принимает: Дизайнер интерьера
О-11	объект	Обмер	Выездной обмер квартиры: все помещения, проёмы, высоты, стояки, вентканалы, фото стен.	исполнитель		все листы Листы: л. 15 — Обмерный план	акт контрольного обмера; фото с рулеткой и привязкой к стене или углу	К-10 Результат принимает: Архитектор
О-12	По месту	Обмер	Подтвердить на объекте принятое: подрайон климата не задан — принят не северный (жилые от 2,5 м)	Архитектор	±5 мм	Листы, где используется принятая величина. Листы: л. 2–4 — Общие данные	акт контрольного обмера	К-26 Результат принимает: Архитектор
О-13	Кабинет (пом. 1): окно пом. 1, стена Г, дверь пом. 1, стена Б	Обмер	Окно пом. 1, стена Г, дверь пом. 1, стена Б: положение (привязки к ближайшим углам), ширина, высота, высота подоконника, глубина откоса. Принято в проекте: окно: положение, ширина, высота и подоконник приняты по обводу плана заказчика, без обмера, не замерены, проём принят по обводу плана заказчика, без обмера: положение и ширина сняты с плана, не замерены.	Архитектор	±5 мм	Проёмы на обмерном плане и в ведомости проёмов; откосы и оконные работы в ВОР; привязки мебели и выводов к проёмам. Листы: л. 15 — Обмерный план л. 17 — План дверей и ведомость заполнения проёмов	акт контрольного обмера; фото с рулеткой и привязкой к стене или углу	К-1 Результат принимает: Архитектор
О-14	Ванная (пом. 3): дверь пом. 3, стена В	Обмер	Дверь пом. 3, стена В: положение (привязки к ближайшим углам), ширина, высота, толщина стены в проёме. Принято в проекте: проём принят по обводу плана заказчика, без обмера: положение и ширина сняты с плана, не замерены.	Архитектор	±5 мм	Проёмы на обмерном плане и в ведомости проёмов; привязки мебели и выводов к проёмам. Листы: л. 15 — Обмерный план л. 17 — План дверей и ведомость заполнения проёмов	акт контрольного обмера; фото с рулеткой и привязкой к стене или углу	К-1 Результат принимает: Архитектор

Допущения и предложения на листе

Основа листа: планировка по обводу плана заказчика, не замерена (К-1); высота до плиты 2650 мм от чистого пола — решение автора (ИЗ-1); отметки плана потолков сдвинуты на -95 мм (+2.745 плана = низ плиты), не замерено (К-2); толщины стен приняты: наружные 260 мм, перегородки 130 мм (К-1); положение стен и проёмов — по брифу без обмера и плана БТИ (К-1); разрешённая мощность 10 кВт принята, ТУ не переданы (К-6); вентканалы приняты, в брифе не заданы (К-5); тип дома, перекрытие и несущие стены не известны — документов нет (К-3); плита электрическая — принята, в брифе не указано (К-6); система заземления TN-C-S принята, ТУ не переданы (К-6); число жильцов 2 принято, в брифе не указано (К-9); подрайон климата не задан — принят не северный (жилые от 2,5 м) (К-26).

Знак «*» — принято, не замерено и не подтверждено (замерить на объекте): К-4: Ст К1-1, Ст В1-2, Ст Т3-3 — положение стояка снято с обвода плана, не замерено.

См. лист открытых вопросов (лист 5, записи К-1, К-3–К-6, К-9; лист 6, запись К-26).

Изм.	Кол.уч	Лист	№ док.	Подп.	Дата
Разраб.		Кырлан А.С.			04.11.26
Пров.					
ГИП					
Н. контр.					
Утв.					

ГД-2026-020-АИ

Квартира 68 м², элитный модерн

Общая площадь 68,47* м² · * размеры приняты, не замерены (реестр — л. 5–7, К-1)

Дизайн-проект интерьера

Стадия	Лист	Листов
РП	9	105

Задание на контрольный обмер и обследование. Лист 2 из 4

М б/м

Кырлан Александр Сергеевич

выпуск 04.11.2026 № 8be4ef4c81 · стр. 9 из 117

Задание на контрольный обмер и обследование. Лист 3 из 4

ПРЕДВАРИТЕЛЬНО · не для производства работ · открыто пунктов: 25 (реестр — л. 5–7)

Что замерить, вскрыть и получить до заказа материалов и изделий

Этап 1. До демонтажа (продолжение)

№	Где	Способ	Что сделать	Кто выполняет	Точность	Что пересчитается в альбоме	Чем подтверждается	Закрывает вопросы реестра
О-15	Прихожая (пом. 4): дверь пом. 4, стена В	Обмер	Дверь пом. 4, стена В: положение (привязки к ближайшим углам), ширина, высота, толщина стены в проёме. Принято в проекте: входная дверь: положение и ширина проёма приняты по обводу плана заказчика, без обмера, не замерены.	Архитектор	±5 мм	Проёмы на обмерном плане и в ведомости проёмов; привязки мебели и выводов к проёмам. Листы: л. 15 — Обмерный план л. 17 — План дверей и ведомость заполнения проёмов	акт контрольного обмера; фото с рулеткой и привязкой к стене или углу	К-1 Результат принимает: Архитектор
О-16	Кухня-столовая (пом. 5): окно пом. 5, стена Б, дверь пом. 5, стена Г	Обмер	Окно пом. 5, стена Б, дверь пом. 5, стена Г: положение (привязки к ближайшим углам), ширина, высота, высота подоконника, глубина откоса. Принято в проекте: окно: положение, ширина, высота и подоконник приняты по обводу плана заказчика, без обмера, не замерены, проём принят по обводу плана заказчика, без обмера: положение и ширина сняты с плана, не замерены.	Архитектор	±5 мм	Проёмы на обмерном плане и в ведомости проёмов; откосы и оконные работы в ВОР; привязки мебели и выводов к проёмам. Листы: л. 15 — Обмерный план л. 17 — План дверей и ведомость заполнения проёмов	акт контрольного обмера; фото с рулеткой и привязкой к стене или углу	К-1 Результат принимает: Архитектор
О-17	Гостиная (пом. 6): окно пом. 6, стена Б, дверь пом. 6, стена Г	Обмер	Окно пом. 6, стена Б, дверь пом. 6, стена Г: положение (привязки к ближайшим углам), ширина, высота, высота подоконника, глубина откоса. Принято в проекте: окно: положение, ширина, высота и подоконник приняты по обводу плана заказчика, без обмера, не замерены, проём принят по обводу плана заказчика, без обмера: положение и ширина сняты с плана, не замерены.	Архитектор	±5 мм	Проёмы на обмерном плане и в ведомости проёмов; откосы и оконные работы в ВОР; привязки мебели и выводов к проёмам. Листы: л. 15 — Обмерный план л. 17 — План дверей и ведомость заполнения проёмов	акт контрольного обмера; фото с рулеткой и привязкой к стене или углу	К-1 Результат принимает: Архитектор
О-18	Спальня (пом. 7): окно пом. 7, стена Б, дверь пом. 7, стена А	Обмер	Окно пом. 7, стена Б, дверь пом. 7, стена А: положение (привязки к ближайшим углам), ширина, высота, высота подоконника, глубина откоса. Принято в проекте: окно: положение, ширина, высота и подоконник приняты по обводу плана заказчика, без обмера, не замерены, проём принят по обводу плана заказчика, без обмера: положение и ширина сняты с плана, не замерены.	Архитектор	±5 мм	Проёмы на обмерном плане и в ведомости проёмов; откосы и оконные работы в ВОР; привязки мебели и выводов к проёмам. Листы: л. 15 — Обмерный план л. 17 — План дверей и ведомость заполнения проёмов	акт контрольного обмера; фото с рулеткой и привязкой к стене или углу	К-1 Результат принимает: Архитектор

Допущения и предложения на листе

Основа листа: планировка по обводу плана заказчика, не замерена (К-1); высота до плиты 2650 мм от чистого пола — решение автора (ИЗ-1); отметки плана потолков сдвинуты на -95 мм (+2.745 плана = низ плиты), не замерено (К-2); толщины стен приняты: наружные 260 мм, перегородки 130 мм (К-1); положение стен и проёмов — по брифу без обмера и плана БТИ (К-1); разрешённая мощность 10 кВт принята, ТУ не переданы (К-6); вентканалы приняты, в брифе не заданы (К-5); тип дома, перекрытие и несущие стены не известны — документов нет (К-3); плита электрическая — принята, в брифе не указано (К-6); система заземления TN-C-S принята, ТУ не переданы (К-6); число жильцов 2 принято, в брифе не указано (К-9); подрайон климата не задан — принят не северный (жилые от 2,5 м) (К-26).

См. лист открытых вопросов (лист 5, записи К-1, К-3, К-5, К-6, К-9; лист 6, запись К-26).

Изм.	Кол.уч	Лист	№ док.	Подп.	Дата
Разраб.		Кырлан А.С.			04.11.26
Пров.					
ГИП					
Н. контр.					
Утв.					

ГД-2026-020-АИ

Квартира 68 м², элитный модерн

Общая площадь 68,47* м² · * размеры приняты, не замерены (реестр — л. 5–7, К-1)

Дизайн-проект интерьера

Стадия	Лист	Листов
РП	10	105

Задание на контрольный обмер и обследование.
Лист 3 из 4
М б/м

Кырлан Александр Сергеевич

Задание на контрольный обмер и обследование. Лист 4 из 4

ПРЕДВАРИТЕЛЬНО · не для производства работ · открыто пунктов: 25 (реестр — л. 5–7)

Что замерить, вскрыть и получить до заказа материалов и изделий

Этап 2. После демонтажа, до черновых работ

№	Где	Способ	Что сделать	Кто выполняет	Точность	Что пересчитается в альбоме	Чем подтверждается	Закрывает вопросы реестра
О-19	Кабинет (пом. 1), Санузел (пом. 2), Ванная (пом. 3), Прихожая (пом. 4), Кухня-столовая (пом. 5), Гостиная (пом. 6), Спальня (пом. 7)	Обмер	Нивелировка плиты перекрытия и существующего пола после демонтажа покрытий: отметки в углах и по сетке, перепады по помещению, уклоны, отметки порогов (чистый пол в мокрых зонах принят -15 мм, 0 мм). Принятая толщина стяжки 33 мм, 50 мм и отметка чистого пола — расчётные, не от замера плиты.	Архитектор	±5 мм по отметке; ровность просвет под 2-метровой рейкой, горизонталь против 0,2 % длины помещения	Толщина стяжки и отметка чистого пола; уклоны к трапам и пороги; выпуски К1 относительно чистого пола (план разводки); объёмы стяжки и смеси в ВОР и спецификации. Листы: л. 49, 53 — План полов л. 35 — Схема разводки водопровода и канализации	акт контрольного обмера	Вопроса в реестре нет: Альбом принимает отметки плиты и толщину пирога пола без нивелировки. Результат принимает: Отделочник
О-20	Кабинет (пом. 1), Санузел (пом. 2), Ванная (пом. 3), Прихожая (пом. 4), Кухня-столовая (пом. 5), Гостиная (пом. 6), Спальня (пом. 7)	Обмер	Вертикаль и плоскостность стен: отклонение от вертикали по высоте стены (отвес или лазерный уровень), просвет под правилом 2 м, кривизна углов. Нужно там, где от стены зависит изделие: облицовка плиткой (пом. 2, 3), штукатурка и окраска (пом. 1, 2, 3, 4, 5, 6, 7), встроенная мебель и кухня (пом. 4, 5).	Архитектор	до 1 мм на 2 м (правило и клиновой щуп); вертикаль — мм на высоту стены, отклонения подписываются на плане	Толщина штукатурки и расход смеси в ВОР и спецификации; раскладка плитки (подрезка у стен); зазоры и крепление встроенной мебели и кухни. Листы: л. 49–52 — Раскладка плитки л. 54, 55 — Ведомость отделки помещений	акт контрольного обмера	Вопроса в реестре нет: Альбом принимает стены ровными и вертикальными без замера. Результат принимает: Отделочник

Документы и данные закупки (не на объекте)

№	У кого, откуда	Способ	Что получить	К какому сроку	Что пересчитается в альбоме	Чем подтверждается	Закрывает вопросы реестра
О-21	заказчик	Документ	План БТИ (поэтажный план с экспликацией) или проект дома АР.	до демонтажа	обмерный план, планировка, расстановка мебели Листы: л. 15 — Обмерный план л. 17 — План дверей и ведомость заполнения проёмов л. 19 — План расстановки мебели	копия документа	К-1 Результат принимает: Архитектор
О-22	заказчик; УК или застройщик	Документ	Проект дома (АР, КР) или план БТИ с несущими конструкциями; тип дома и перекрытие.	до демонтажных работ	несущие стены, допустимость демонтажа, нагрузки от перегородок Листы: л. 15 — Обмерный план л. 16 — План демонтажа и монтажа перегородок	копия документа	К-3 Результат принимает: Архитектор
О-23	заказчик, УК	Документ	ТУ на электроснабжение или справка УК о разрешённой мощности и вводном автомате.	до сборки щита	вводной автомат, группы варочной панели и духового шкафа Листы: л. 28 — Однолинейная схема щита	копия документа	К-6 Результат принимает: Инженер-электрик
О-24	адрес объекта, СП 131.13330	Документ	Климатический подрайон по СП 131.13330 (по адресу объекта)	до заказа каркаса потолков	план потолков, разрезы, ведомость объёмов Листы: л. 45 — План потолков	копия документа	К-26 Результат принимает: Архитектор

Примечания

1. Подтверждение: акт контрольного обмера (дата, кто присутствовал, прибор, перечень промеров с результатами, подписи присутствующих); к акту — фото вскрытий и узлов и техническое заключение организации, выполнившей обследование.
2. Номера листов — по ведомости рабочих чертежей комплекта (лист «Общие данные»).
3. Пункт исключается из задания при следующем выпуске, когда акт подписан, значение внесено в проект и листы перевыпущены; знак «*» у величины снимается только замером.

Допущения и предложения на листе

Основа листа: планировка по обводу плана заказчика, не замерена (К-1); высота до плиты 2650 мм от чистого пола — решение автора (ИЗ-1); отметки плана потолков сдвинуты на -95 мм (+2.745 плана = низ плиты), не замерено (К-2); толщины стен приняты: наружные 260 мм, перегородки 130 мм (К-1); положение стен и проёмов — по брифу без обмера и плана БТИ (К-1); разрешённая мощность 10 кВт принята, ТУ не переданы (К-6); вентканалы приняты, в брифе не заданы (К-5); тип дома, перекрытие и несущие стены не известны — документов нет (К-3); плита электрическая — принята, в брифе не указано (К-6); система заземления TN-C-S принята, ТУ не переданы (К-6); число жильцов 2 принято, в брифе не указано (К-9); подрайон климата не задан — принят не северный (жилые от 2,5 м) (К-26).
См. лист открытых вопросов (лист 5, записи К-1, К-3, К-5, К-6, К-9; лист 6, запись К-26).

Изм.	Кол.уч	Лист	№ док.	Подп.	Дата
Разраб.		Кырлан А.С.			04.11.26
Пров.					
ГИП					
Н. контр.					
Утв.					

ГД-2026-020-АИ

Квартира 68 м², элитный модерн

Общая площадь 68,47* м² · * размеры приняты, не замерены (реестр — л. 5–7, К-1)

Дизайн-проект интерьера

Стадия	Лист	Листов
РП	11	105

Задание на контрольный обмер и обследование.
Лист 4 из 4
М б/м

Кырлан Александр Сергеевич

выпуск 04.11.2026 № 8be4ef4c81 · стр. 11 из 117

График закупок и работ. Лист 1 из 3

ПРЕДВАРИТЕЛЬНО · не для производства работ · открыто пунктов: 25 (реестр — л. 5–7)

Что заказывать и когда не раньше чего: относительный порядок без дат; срок поставки — из данных или «не задан» с записью реестра

Лист не содержит дат: контрольного обмера, подписанных решений автора и договоров ещё нет, и любая дата была бы выдумана. Вместо календаря — порядок и условия: замер → решение и выбор изделия → заказ → срок поставки → работа, которую позиция блокирует. Срок поставки печатается как срок, только если он задан в данных позиции. Нет — «срок поставки не задан» и ссылка на вопрос реестра о сроках; типовой диапазон практики стоит рядом как ориентир и заказывать по нему нельзя. Номера З-N и Р-N — строки этого листа, К-N — записи реестра открытых вопросов, О-N — позиции задания на контрольный обмер.

Закупки: что заказывается, от чего зависит заказ и какую работу блокирует

№	Позиция и где	1. Замер до заказа	2. Решение, выбор изделия, паспорт	3. Условие заказа	4. Срок поставки	5. Блокирует работу	Закрывает вопросы реестра
З-1	Кухонный гарнитур по проекту кухни: модули М7**, М8, М9, М10, М11**, М12, М13, М14, М15, М16, М17 пом. 5			После 1 и 2 и после получения срока у поставщика (вопроса о сроках нет); дата заказа — когда срок известен, не позднее чем за срок до начала Р-15.	срок поставки не задан (записи реестра нет) Ориентир практики (не срок поставщика): 4–8 нед. от замера	Р-15 «кухня и мебель»: замер кухни — по готовым стенам после штукатурки или плитки, до чистового пола; производство идёт параллельно со стяжкой и отделкой	
З-2	Встраиваемая техника кухни: М7** холодильник, М9 oven, М12 посудомоечная машина, М14 вытяжка пом. 5			После 1 и 2 и после получения срока у поставщика (вопроса о сроках нет); дата заказа — когда срок известен, не позднее чем за срок до начала Р-15.	срок поставки не задан (записи реестра нет)	Р-15 «кухня и мебель»: паспорта и монтажные схемы — до изготовления модулей кухни: нишу и вентзазоры задаёт модель, а не типовая схема 60 см	
З-3	Стиральная машина: П16** (вертикальная загрузка 400 × 600 мм — условие закупки) пом. 3			После 1 и 2 и после получения срока у поставщика (вопроса о сроках нет); дата заказа — когда срок известен, не позднее чем за срок до начала Р-4.	срок поставки не задан (записи реестра нет)	Р-4 «черновая сантехника»: габарит и подводка — до закрытия люка и разводки	
З-4	Сантехнические приборы и инсталляции: П4, П7, П9**, П10**, П1 пом. 2, 3, 5	О-5: обмер: Ванная (пом. 3): Ст К1-1*, Ст В1-2, Ст Т3-3*; наличие стояка ГВС, арматуры и счётчиков — по всей квартире (К-4); до разводки О-2: обмер: у окон		После 1 и 2 и после получения срока у поставщика (вопроса о сроках нет); дата заказа — когда срок известен, не позднее чем за срок до начала Р-4.	срок поставки не задан (записи реестра нет)	Р-4 «черновая сантехника»: инсталляцию ставят до обшивки ГКЛВ и до гидроизоляции стены	К-4
З-5	Керамогранит и плитка: 4 поз. по артикулу и формату, 51,59 м² по раскладке пом. 2, 3, 4, 5	О-19: обмер: Кабинет (пом. 1), Санузел (пом. 2), Ванная (пом. 3), Прихожая (пом. 4), Кухня-столовая (пом. 5), Гостиная (пом. 6), Спальня (пом. 7) О-20: обмер: Кабинет (пом. 1), Санузел (пом. 2), Ванная (пом. 3), Прихожая (пом. 4), Кухня-столовая (пом. 5), Гостиная (пом. 6), Спальня (пом. 7)		После 1 и 2 и после получения срока у поставщика (вопроса о сроках нет); дата заказа — когда срок известен, не позднее чем за срок до начала Р-9.	срок поставки не задан (записи реестра нет)	Р-9 «плитка»: калибр партии измеряют до раскладки, раскладку пересчитывают до заказа	
З-6	Покрытие пола (доска) и плинтус: пом. 1, 5, 6, 7 пом. 1, 5, 6, 7	О-19: обмер: Кабинет (пом. 1), Санузел (пом. 2), Ванная (пом. 3), Прихожая (пом. 4), Кухня-столовая (пом. 5), Гостиная (пом. 6), Спальня (пом. 7)		После 1 и 2 и после получения срока у поставщика (вопроса о сроках нет); дата заказа — когда срок известен, не позднее чем за срок до начала Р-12.	срок поставки не задан (записи реестра нет)	Р-12 «чистовые полы»: артикул и партия — до заказа; доску привозят к чистовым полам	
З-7	Встроенная мебель по замеру цеха: М5** пом. 4	О-3: обмер: все помещения, обход по часовой стрелке от входа (К-1); до заказа мебели и дверей		После 1 и 2 и после получения срока у поставщика (вопроса о сроках нет); дата заказа — когда срок известен, не позднее чем за срок до начала Р-15.	срок поставки не задан (записи реестра нет) Ориентир практики (не срок поставщика): 4–8 нед. от замера	Р-15 «кухня и мебель»: цех замеряет по готовым стенам; производство 4–8 недель идёт параллельно с отделкой	К-1

Допущения и предложения на листе

Основа листа: планировка по обводу плана заказчика, не замерена (К-1); высота до плиты 2650 мм от чистого пола — решение автора (ИЗ-1); отметки плана потолков сдвинуты на -95 мм (+2.745 плана = низ плиты), не замерено (К-2); толщины стен приняты: наружные 260 мм, перегородки 130 мм (К-1); положение стен и проёмов — по брифу без обмера и плана БТИ (К-1); разрешённая мощность 10 кВт принята, ТУ не переданы (К-6); вентканалы приняты, в брифе не заданы (К-5); тип дома, перекрытие и несущие стены не известны — документов нет (К-3); плита электрическая — принята, в брифе не указано (К-6); система заземления TN-C-S принята, ТУ не переданы (К-6); число жильцов 2 принято, в брифе не указано (К-9); подрайон климата не задан — принят не северный (жилые от 2,5 м) (К-26).

Знак «*» — принято, не замерено и не подтверждено (замерить на объекте): К-4: Ст К1-1, Ст Т3-3 — положение стояка снято с обвода плана, не замерено.

Знак «**» — предложение проектировщика, заказчиком не утверждено (согласовать с заказчиком): ИЗ-3, К-7: П10 — раковина у левой стены: светильники 14 плана — у зеркала над ней; отвод К1 к стояку в углу короткий; П16 — место стиральной машины — в ванной у верхней стены, правее короба стояка; подход 1100 мм перед дверцей, выводы ХВС и К1 Ø40 за машиной; ИЗ-3, К-28: П9 — ванна 1700 × 750 у правой стены на всю глубину помещения (1700 мм по плану) — стояк в левом углу свободен; К-7: М5, М7, М11.

См. лист открытых вопросов (лист 5, записи К-1, К-3–К-7, К-9; лист 6, запись К-26; лист 7, записи ИЗ-3, К-28).

Изм.	Кол.уч	Лист	№ док.	Подп.	Дата
Разраб.		Кырлан А.С.			04.11.26
Пров.					
ГИП					
Н. контр.					
Утв.					

ГД-2026-020-АИ

Квартира 68 м², элитный модерн

Общая площадь 68,47* м² · * размеры приняты, не замерены (реестр — л. 5–7, К-1)

Дизайн-проект интерьера

Стадия	Лист	Листов
РП	12	105

График закупок и работ. Лист 1 из 3

М б/м

Кырлан Александр Сергеевич

выпуск 04.11.2026 № 8be4ef4c81 · стр. 12 из 117

График закупок и работ. Лист 2 из 3

ПРЕДВАРИТЕЛЬНО · не для производства работ · открыто пунктов: 25 (реестр — л. 5–7)

Что заказывать и когда не раньше чего: относительный порядок без дат; срок поставки — из данных или «не задан» с записью реестра

Работы: порядок и что не даёт начать

№	Работа (стадия технологической последовательности)	После	Что должно быть к началу: условия и закупки	Не начинать, пока открыто в реестре
Р-1	Демонтаж покрытий, отделки стен и потолков, дверных блоков и приборов; конструкции, стены и перегородки не трогать до технического заключения (стадия 1)		до начала: запрошены документы на дом и БТИ; контрольный обмер до демонтажа (что видно) сделан	
Р-2	Контрольный обмер на голых стенах и обследование (задание — лист «Задание на контрольный обмер») (стадия 2)	Р-1	после снятия отделки: видны стояки, каналы, щиток, толщины стен; до заказа всего, что делают по размеру	
Р-3	Черновая электрика: штробы, короба, гофра, подрозетники, щит (стадия 4)	Р-2	до начала: план электрики с высотами утверждён; штробы в стенах — только после технического заключения; мебель расставлена	К-6: Разрешённая мощность по ТУ в брифе не указана; принята 10 кВт (квартира с электроплитой).
Р-4	Черновая сантехника и вентиляция: разводка, выводы, инсталляции, короба стояков (стадия 5)	Р-2	до начала: положение стояков замерено; модели инсталляций и машины выбраны (габариты рамы, подводка); инсталляцию ставят до обшивки ГКЛВ и до гидроизоляции Закупки к началу: З-3 (стиральная машина), З-4 (сантехника)	К-4: Стояки: на плане потолков есть только знак ∅ в верхнем левом углу ванной (120 мм от стены) — принят за стояк канализации К1 Ø110; стояки В1 и Т3 на плане не показаны и приняты в том же коробе (предложение).
Р-5	Коробки скрытых дверей, затем штукатурка стен и откосов (стадия 6)	Р-2, Р-3, Р-4	до начала: электрика и сантехника смонтированы, штробы заделаны; коробки скрытых дверей установлены до штукатурки (поэтому заказ дверей — раньше работы)	
Р-6	Стяжка пола и тёплый пол (стадия 7)	Р-5	до начала: штукатурка сделана; трубы под стяжкой приняты; нивелировка плиты выполнена	
Р-7	Гидроизоляция санузлов и тест проливом (стадия 8)	Р-6	до начала: стяжка набрала прочность и сухая по инструкции гидроизоляции; выводы стоят на проектных отметках	
Р-8	ГКЛ: короба инсталляции и стояков, ниши, потолки (стадия 9)	Р-3, Р-4	до начала: черновые сети в зоне коробов приняты; закладные под тяжёлое и карнизы стоят; светильники выбраны (вырезы)	
Р-9	Плитка и керамогранит: стены, затем пол; фартук (стадия 10)	Р-6, Р-7, Р-8	до начала: гидроизоляция принята; плитка выбрана, калибр партии измерен, раскладка пересчитана и подписана Закупки к началу: З-5 (плитка)	

Допущения и предложения на листе

Основа листа: планировка по обводу плана заказчика, не замерена (К-1); высота до плиты 2650 мм от чистого пола — решение автора (ИЗ-1); отметки плана потолков сдвинуты на -95 мм (+2.745 плана = низ плиты), не замерено (К-2); толщины стен приняты: наружные 260 мм, перегородки 130 мм (К-1); положение стен и проёмов — по брифу без обмера и плана БТИ (К-1); разрешённая мощность 10 кВт принята, ТУ не переданы (К-6); вентканалы приняты, в брифе не заданы (К-5); тип дома, перекрытие и несущие стены не известны — документов нет (К-3); плита электрическая — принята, в брифе не указано (К-6); система заземления TN-C-S принята, ТУ не переданы (К-6); число жильцов 2 принято, в брифе не указано (К-9); подрайон климата не задан — принят не северный (жилые от 2,5 м) (К-26).

См. лист открытых вопросов (лист 5, записи К-1, К-3, К-5, К-6, К-9; лист 6, запись К-26).

Изм.	Кол.уч	Лист	№ док.	Подп.	Дата
Разраб.		Кырлан А.С.			04.11.26
Пров.					
ГИП					
Н. контр.					
Утв.					

ГД-2026-020-АИ

Квартира 68 м², элитный модерн

Общая площадь 68,47* м² · * размеры приняты, не замерены (реестр — л. 5–7, К-1)

Дизайн-проект интерьера

Стадия	Лист	Листов
РП	13	105

График закупок и работ. Лист 2 из 3

М б/м

Кырлан Александр Сергеевич

выпуск 04.11.2026 № 8be4ef4c81 · стр. 13 из 117

График закупок и работ. Лист 3 из 3

ПРЕДВАРИТЕЛЬНО · не для производства работ · открыто пунктов: 25 (реестр — л. 5–7)

Что заказывать и когда не раньше чего: относительный порядок без дат; срок поставки — из данных или «не задан» с записью реестра

Работы: порядок и что не даёт начать (продолжение)

№	Работа (стадия технологической последовательности)	После	Что должно быть к началу: условия и закупки	Не начинать, пока открыто в реестре
Р-10	Шпаклёвка стен и потолков под окраску (стадия 11)	Р-5, Р-8, Р-9	до начала: плитка готова (грязные работы закончены); штукатурка и ГКЛ сухие	
Р-11	Окраска стен, потолков, откосов (стадия 13)	Р-10	до начала: шпаклёвка отшлифована и огрунтована; выкрасы утверждены, колеровка одной партией	
Р-12	Чистовые полы: инженерная доска (стадия 14)	Р-9, Р-11	до начала: влажность основания в норме, мокрые работы закончены; доска выбрана и привезена Закупки к началу: З-6 (доска и плинтус)	
Р-13	Полотна межкомнатных дверей, плинтусы, пороги (стадия 15)	Р-11, Р-12	до начала: чистовой пол уложен; полотна скрытых дверей — после чистовой отделки стен	
Р-14	Чистовая электрика и сантехника: механизмы, светильники, смесители, приборы (стадия 16)	Р-11, Р-13	до начала: отделка готова; механизмы, светильники и приборы выбраны и привезены	
Р-15	Кухня, встроенная и корпусная мебель, бытовая техника (стадия 17)	Р-13, Р-14	до начала: чистовая сантехника и электрика подведены к местам мебели; замер кухни снят по готовым стенам (после штукатурки или плитки, до чистового пола) Закупки к началу: З-1 (кухонный гарнитур), З-2 (техника кухни), З-7 (мебель по замеру)	К-1: Планировка принята по обводу плана заказчика, без обмера: план заказчика распознан автоматически по картинке (1 модель ИИ, масштаб — размерные цепочки), затем исправлен исполнителем вручную по размерным числам и рисунку плана (15 правок) и не проверен дизайнером: положение помещений, стен и проёмов — по обводу, контрольный обмер на объекте не выполнялся.
Р-16	Сдача: осмотр по чек-листу, дефектная ведомость, устранение замечаний (стадия 18)	Р-14, Р-15	до начала: всё смонтировано; акты скрытых работ подписаны	

Примечания

1. Порядок работ — стадии технологической последовательности из 16 позиций, присутствующих в этом проекте (по строкам ведомости объёмов); остальные стадии таблицы knowledge/remont-tehnologiya.md в проекте не встречаются. Длительности работ не печатаются: их нет ни в данных, ни в нормах для этого объекта.
2. Типовые сроки — ориентир практики, не срок поставщика: скрытые двери — короб около 10 дн., полотно под покраску до 3 нед., шпон 4–5 нед., в среднем около 30 дн. (knowledge/workers/foreman.md, п. 2.4 (profil-doors)); кухня и корпусная мебель — 4–8 недель от замера (knowledge/remont-tehnologiya.md, разд. 2; knowledge/workers/foreman.md, п. 2.4). Заказ по ориентиру не назначается: срок получают у поставщика (вопрос реестра), после чего заказ планируют «не позднее чем за срок до начала работы».
3. Условия заказа берутся из реестра открытых вопросов и задания на контрольный обмер: позиция заказывается, когда закрыты замер (графа 1) и решение (графа 2). Закрывать их может только факт или решение автора с подписью; снять строку с листа можно только закрыв запись реестра.
4. Заказ по размеру до контрольного обмера не делают: двери, кухня и встроенная мебель зависят от обмера (К-11, К-13); скрытые двери, кроме того, зависят от решения по нише санузла 2 (проём Д-5 в перегородке П-1).
5. Номера листов — по ведомости рабочих чертежей комплекта (лист «Общие данные»).

Допущения и предложения на листе

Основа листа: планировка по обводу плана заказчика, не замерена (К-1); высота до плиты 2650 мм от чистого пола — решение автора (ИЗ-1); отметки плана потолков сдвинуты на -95 мм (+2.745 плана = низ плиты), не замерено (К-2); толщины стен приняты: наружные 260 мм, перегородки 130 мм (К-1); положение стен и проёмов — по брифу без обмера и плана БТИ (К-1); разрешённая мощность 10 кВт принята, ТУ не переданы (К-6); вентканалы приняты, в брифе не заданы (К-5); тип дома, перекрытие и несущие стены не известны — документов нет (К-3); плита электрическая — принята, в брифе не указано (К-6); система заземления TN-C-S принята, ТУ не переданы (К-6); число жильцов 2 принято, в брифе не указано (К-9); подрайон климата не задан — принят не северный (жилые от 2,5 м) (К-26).
См. лист открытых вопросов (лист 5, записи К-1, К-3, К-5, К-6, К-9; лист 6, запись К-26).

Изм.	Кол.уч	Лист	№ док.	Подп.	Дата
Разраб.		Кырлан А.С.			04.11.26
Пров.					
ГИП					
Н. контр.					
Утв.					

ГД-2026-020-АИ

Квартира 68 м², элитный модерн

Общая площадь 68,47* м² · * размеры приняты, не замерены (реестр — л. 5–7, К-1)

Дизайн-проект интерьера

Стадия	Лист	Листов
РП	14	105

График закупок и работ. Лист 3 из 3

М б/м

Кырлан Александр Сергеевич

выпуск 04.11.2026 № 8be4ef4c81 · стр. 14 из 117

01

Архитектурные решения

Кырлан Александр Сергеевич

выпуск 04.11.2026 № 8be4ef4c81 · стр. 15 из 117


Обмерный план

Существующее положение · размеры в мм · отметки от чистого пола

ПРЕДВАРИТЕЛЬНО · не для производства работ · открыто пунктов: 25 (реестр — л. 5–7)

Отметки по высоте

±0,000	чистый пол пом. 1, 4–7; отсчёт высот
−0,015	чистый пол пом. 2, 3, ниже на 15 мм
−0,064*	верх плиты — расчёт, не замер (задание на обмер)
сущ. пол	снимается до плиты; не замерен (задание на обмер)

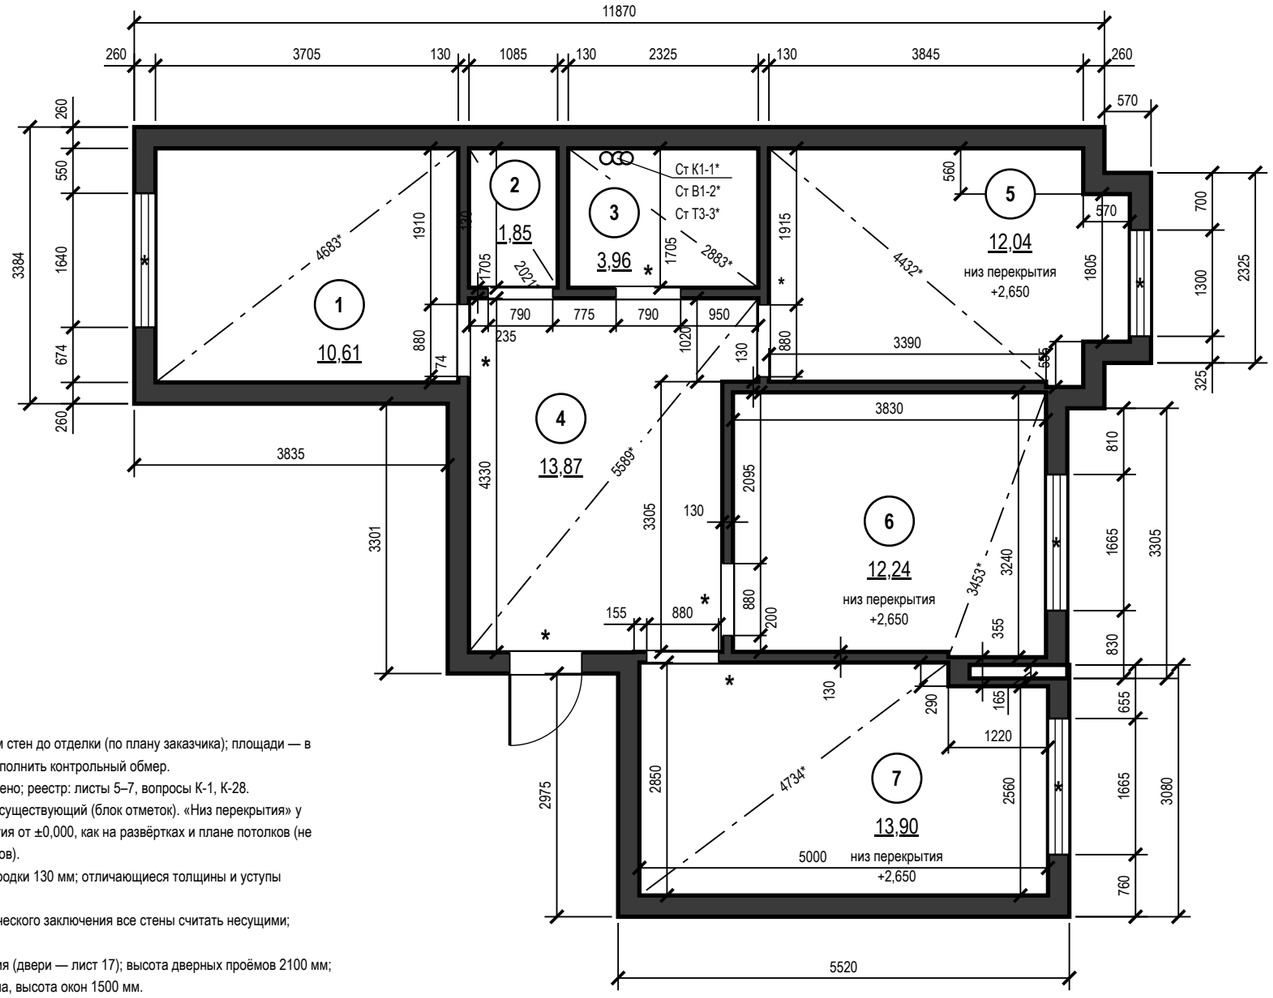

Экспликация помещений

№	Наименование	Площадь, м²
1	Кабинет	10,61
2	Санузел	1,85
3	Ванная	3,96
4	Прихожая	13,87
5	Кухня-столовая	12,04
6	Гостиная	12,24
7	Спальня	13,90
	Итого (общая площадь)	**68,47**

Условные обозначения

- существующие стены (сечение)
- окно (рама, остекление)
- проём существующий, без заполнения (откосы)
- стояк: К1 — канализация, В1 — ХВС, Т3 — ГВС
- ** — «**» — предложение проектировщика, заказчиком не утверждено
- диагональ помещения — контроль прямоугольности
- (1) — номер помещения, площадь м²
- * — «*» — принято, не замерено и не подтверждено

Примечания

1. Размеры — в мм по чистым поверхностям стен до отделки (по плану заказчика); площади — в м² по тем же размерам. До начала работ выполнить контрольный обмер.
2. Знак «*» у проёма — положение не замерено; реестр: листы 5–7, вопросы К-1, К-28.
3. За отметку ±0,000 принят чистый пол, не существующий (блок отметок). «Низ перекрытия» у марки помещения — отметка низа перекрытия от ±0,000, как на развёртках и плане потолков (не высота потолка: потолок — по плану потолков).
4. Толщины стен: наружные 260 мм, перегородки 130 мм; отличающиеся толщины и уступы размерами на плане.
5. Несущие стены не определены: до технического заключения все стены считать несущими; проёмы и штробы в них не выполнять.
6. Дверные проёмы показаны без заполнения (двери — лист 17); высота дверных проёмов 2100 мм; низ окон (подоконник) 900 мм от чистого пола, высота окон 1500 мм.
7. Диагонали — контрольные размеры; «*» — расчёт по принятому контуру (К-1), при обмере заменить замеренным; расхождение более 5 мм подписать на плане как перекос.
8. Размеры проверить на месте до начала работ; расхождение контрольных промеров ≤ 2 %.
9. Размеры короче 1 мм на листе цепочкой не показаны (две выносные линии на таком расстоянии сливаются): пом. 4, стена В — 45 мм от проёма до угла; пом. 5, стена Г — 60 мм от проёма до угла.

Допущения и предложения на листе

Основа листа: планировка по обводу плана заказчика, не замерена (К-1); высота до плиты 2650 мм от чистого пола — решение автора (ИЗ-1); отметки плана потолков сдвинуты на -95 мм (+2.745 плана = низ плиты), не замерено (К-2); толщины стен приняты: наружные 260 мм, перегородки 130 мм (К-1); положение стен и проёмов — по брифу без обмера и плана БТИ (К-1); разрешённая мощность 10 кВт принята, ТУ не переданы (К-6); вентканалы приняты, в брифе не заданы (К-5); тип дома, перекрытие и несущие стены не известны — документов нет (К-3); плита электрическая — принята, в брифе не указано (К-6); система заземления TN-C-S принята, ТУ не переданы (К-6); число жильцов 2 принято, в брифе не указано (К-9); подрайон климата не задан — принят не северный (жилые от 2,5 м) (К-26).

Знак «*» — принято, не замерено и не подтверждено (замерить на объекте): К-1: окно пом. 1 (стена Г), 5 (Б), 6 (Б), 7 (Б) — окно: положение, ширина, высота и подоконник приняты по обводу плана заказчика, без обмера, не замерены; дверь пом. 1 (стена Б), 3 (В), 5 (Г), 6 (Г), 7 (А) — проём принят по обводу плана заказчика, без обмера: положение и ширина сняты с плана, не замерены; дверь пом. 4 (стена В) — входная дверь: положение и ширина проёма приняты по обводу плана заказчика, без обмера, не замерены; К-4: Ст К1-1, Ст В1-2, Ст Т3-3 — положение стояка снято с обвода плана, не замерено.

Знак «**» — предложение проектировщика, заказчиком не утверждено (согласовать с заказчиком): К-1: дверь пом. 2 (стена В) — проём принят по обводу плана заказчика, без обмера: положение и ширина сняты с плана, не замерены; открывание наружу (в прихожую): санузел 1,1 м — внутрь полотно задевает раковину П14.

Открытые вопросы и конфликты по листу: К-1, К-3, К-10, К-14–К-19.

См. лист открытых вопросов (лист 5, записи К-1, К-3–К-6, К-9, К-10, К-14–К-16; лист 6, записи К-17–К-19, К-26).

Принято, не определено или спорно

полностью — листы 5–7

К-3 — Тип дома, конструкция перекрытия и несущие стены в брифе не указаны; проект дома, план БТИ и техническое заключение не переданы

К-10 — Заказчик указал в брифе, что плана нет и нужен обмер: все размеры альбома до обмера — допущение

К-14 — Эркер кухни образмерен частично: окно 1300 мм, глубина ≈ 570 мм, скос к нижней стене ≈ 45° (на листе не образмерен, по рисунку ≈ 1150 мм, вероятно, тоже остеклён)

К-15 — В верхней (наружной?) стене кухни на плане два узких разрыва ≈ 130 мм (над лентой 13) с участком стены 650 мм между ними

К-16 — Входная дверь на плане не помечена (марки Д-1…Д-5 — межкомнатные)

К-17 — Проём из прихожей в спальню (880 мм) без марки Д — это проём без двери или дверь, не попавшая в ведомость Д?

К-18 — В правом верхнем углу спальни прямоугольник ≈ 1300 × 290 мм вне контура потолка (без подписи): короб, шахта, ниша, колонна?

К-19 — У левой стены кухни рядом с Д-4 на плане синий участок «залізобетон» ≈ 640 × 90 мм (выступ несущей стены или колонна?)

1000 мм · печать 1:1

Изм.	Кол.уч	Лист	№ док.	Подп.	Дата
Разраб.		Кырлан А.С.			04.11.26
Пров.					
ГИП					
Н. контр.					
Утв.					

ГД-2026-020-АИ

Квартира 68 м², элитный модерн

Общая площадь 68,47* м² · * размеры приняты, не замерены (реестр — л. 5–7, К-1)

Дизайн-проект интерьера

Стадия	Лист	Листов
РП	15	105

Обмерный план

М 1:75

Кырлан Александр Сергеевич

выпуск 04.11.2026 № 8be4ef4c81 · стр. 16 из 117


План демонтажа и монтажа перегородок

Перепланировка не выполняется · существующие стены сохраняются · размеры в мм

ПРЕДВАРИТЕЛЬНО · не для производства работ · открыто пунктов: 25 (реестр — л. 5–7)

Условные обозначения


- существующие стены — сохраняются;
- несущие не определены — считать несущими
- демонтируемые конструкции — на плане нет
- возводимые перегородки — на плане нет
- проём существующий, без заполнения (откосы)
- 1 — номер помещения, площадь м²
- * — «*» — принято, не замерено и не подтверждено

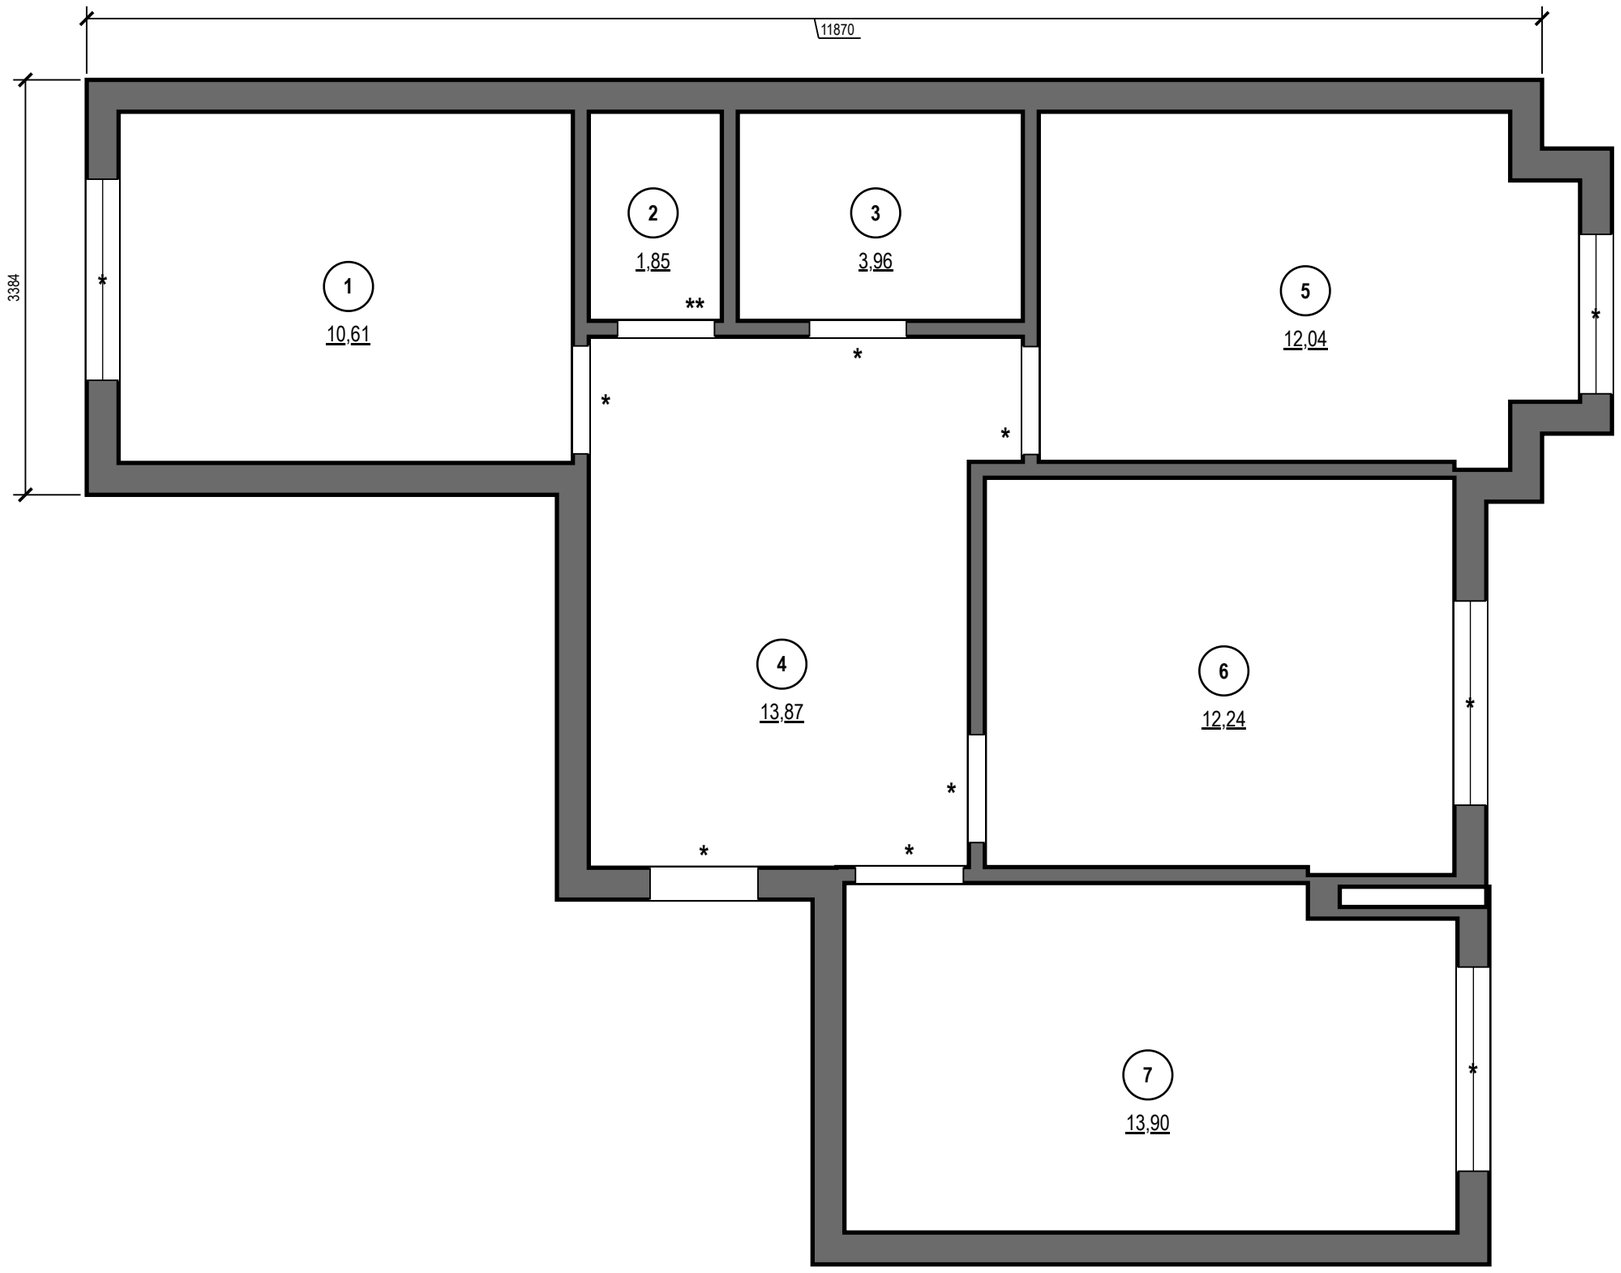

Примечания

1. Перепланировка не выполняется: несущие и ненесущие стены, перегородки и плиты перекрытия не демонтируются, новые стены не возводятся; существующие стены и перегородки сохраняются.
2. Дверные блоки — по плану дверей (лист 17); существующие проёмы не расширяются.
3. Знак «*» — положение проёма не замерено: окна пом. 1, 5, 6, 7; двери пом. 1, 3, 4, 5, 6, 7. Реестр: листы 5–7, вопросы К-1, К-28.
4. Демонтаж существующих покрытий пола, стен и потолка, дверных блоков и сантехприборов (если есть) — до основания; объёмы демонтажа — для справки, по факту на объекте.
5. За отметку ±0,000 принят чистый пол, не существующий (блок отметок). Размеры — в мм по чистовой поверхности стен до отделки.
6. Размеры проверить на месте до начала работ: расхождение с обмером — не более 2 % (иначе — к архитектору).
7. Несущие стены не определены: до технического заключения все стены считать несущими — проёмы, ниши и штробы в них не выполнять.

Отметки по высоте

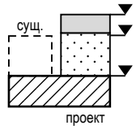

±0,000	чистый пол пом. 1, 4–7; отсчёт высот
−0,015	чистый пол пом. 2, 3, ниже на 15 мм
−0,064*	верх плиты — расчёт, не замер (задание на обмер)
сущ. пол	снимается до плиты; не замерен (задание на обмер)

Допущения и предложения на листе

Основа листа: планировка по обводу плана заказчика, не замерена (К-1); высота до плиты 2650 мм от чистого пола — решение автора (ИЗ-1); отметки плана потолков сдвинуты на -95 мм (+2.745 плана = низ плиты), не замерено (К-2); толщины стен приняты: наружные 260 мм, перегородки 130 мм (К-1); положение стен и проёмов — по брифу без обмера и плана БТИ (К-1); разрешённая мощность 10 кВт принята, ТУ не переданы (К-6); вентканалы приняты, в брифе не заданы (К-5); тип дома, перекрытие и несущие стены не известны — документов нет (К-3); плита электрическая — принята, в брифе не указано (К-6); система заземления TN-C-S принята, ТУ не переданы (К-6); число жильцов 2 принято, в брифе не указано (К-9); подрайон климата не задан — принят не северный (жилые от 2,5 м) (К-26).

Знак «*» — принято, не замерено и не подтверждено (замерить на объекте): К-1: окно пом. 1 (стена Г), 5 (Б), 6 (Б), 7 (Б) — окно: положение, ширина, высота и подоконник приняты по обводу плана заказчика, без обмера, не замерены; дверь пом. 1 (стена Б), 3 (В), 5 (Г), 6 (Г), 7 (А) — проём принят по обводу плана заказчика, без обмера: положение и ширина сняты с плана, не замерены; дверь пом. 4 (стена В) — входная дверь: положение и ширина проёма приняты по обводу плана заказчика, без обмера, не замерены.

Знак «**» — предложение проектировщика, заказчиком не утверждено (согласовать с заказчиком): К-1: дверь пом. 2 (стена В) — проём принят по обводу плана заказчика, без обмера: положение и ширина сняты с плана, не замерены; открывание наружу (в прихожую): санузел 1,1 м — внутрь полотно задевает раковину П14.

Открытые вопросы и конфликты по листу: К-3.

См. лист открытых вопросов (лист 5, записи К-1, К-3, К-5, К-6, К-9; лист 6, запись К-26).

1000 мм · печать 1:1

Изм.	Кол.уч	Лист	№ док.	Подп.	Дата
Разраб.		Кырлан А.С.			04.11.26
Пров.					
ГИП					
Н. контр.					
Утв.					

ГД-2026-020-АИ

Квартира 68 м², элитный модерн

Общая площадь 68,47* м² · * размеры приняты, не замерены (реестр — л. 5–7, К-1)

Дизайн-проект интерьера

Стадия	Лист	Листов
РП	16	105

План демонтажа и монтажа перегородок

М 1:50

Кырлан Александр Сергеевич


выпуск 04.11.2026 № 8be4ef4c81 · стр. 17 из 117

План дверей и ведомость заполнения проёмов

Проёмы, марки заполнения, привязки · размеры в мм

Условные обозначения

- стены (подложка обмера)
- дверь распашная, дуга открывания
- дверь входная (полотно толще)
- оконный блок
- Д — марка типа (Д-N, ОК-N)
- 1 — номер помещения, площадь м²
- * — «*» — принято, не замерено и не подтверждено
- ** — «**» — предложение проектировщика, заказчиком не утверждено

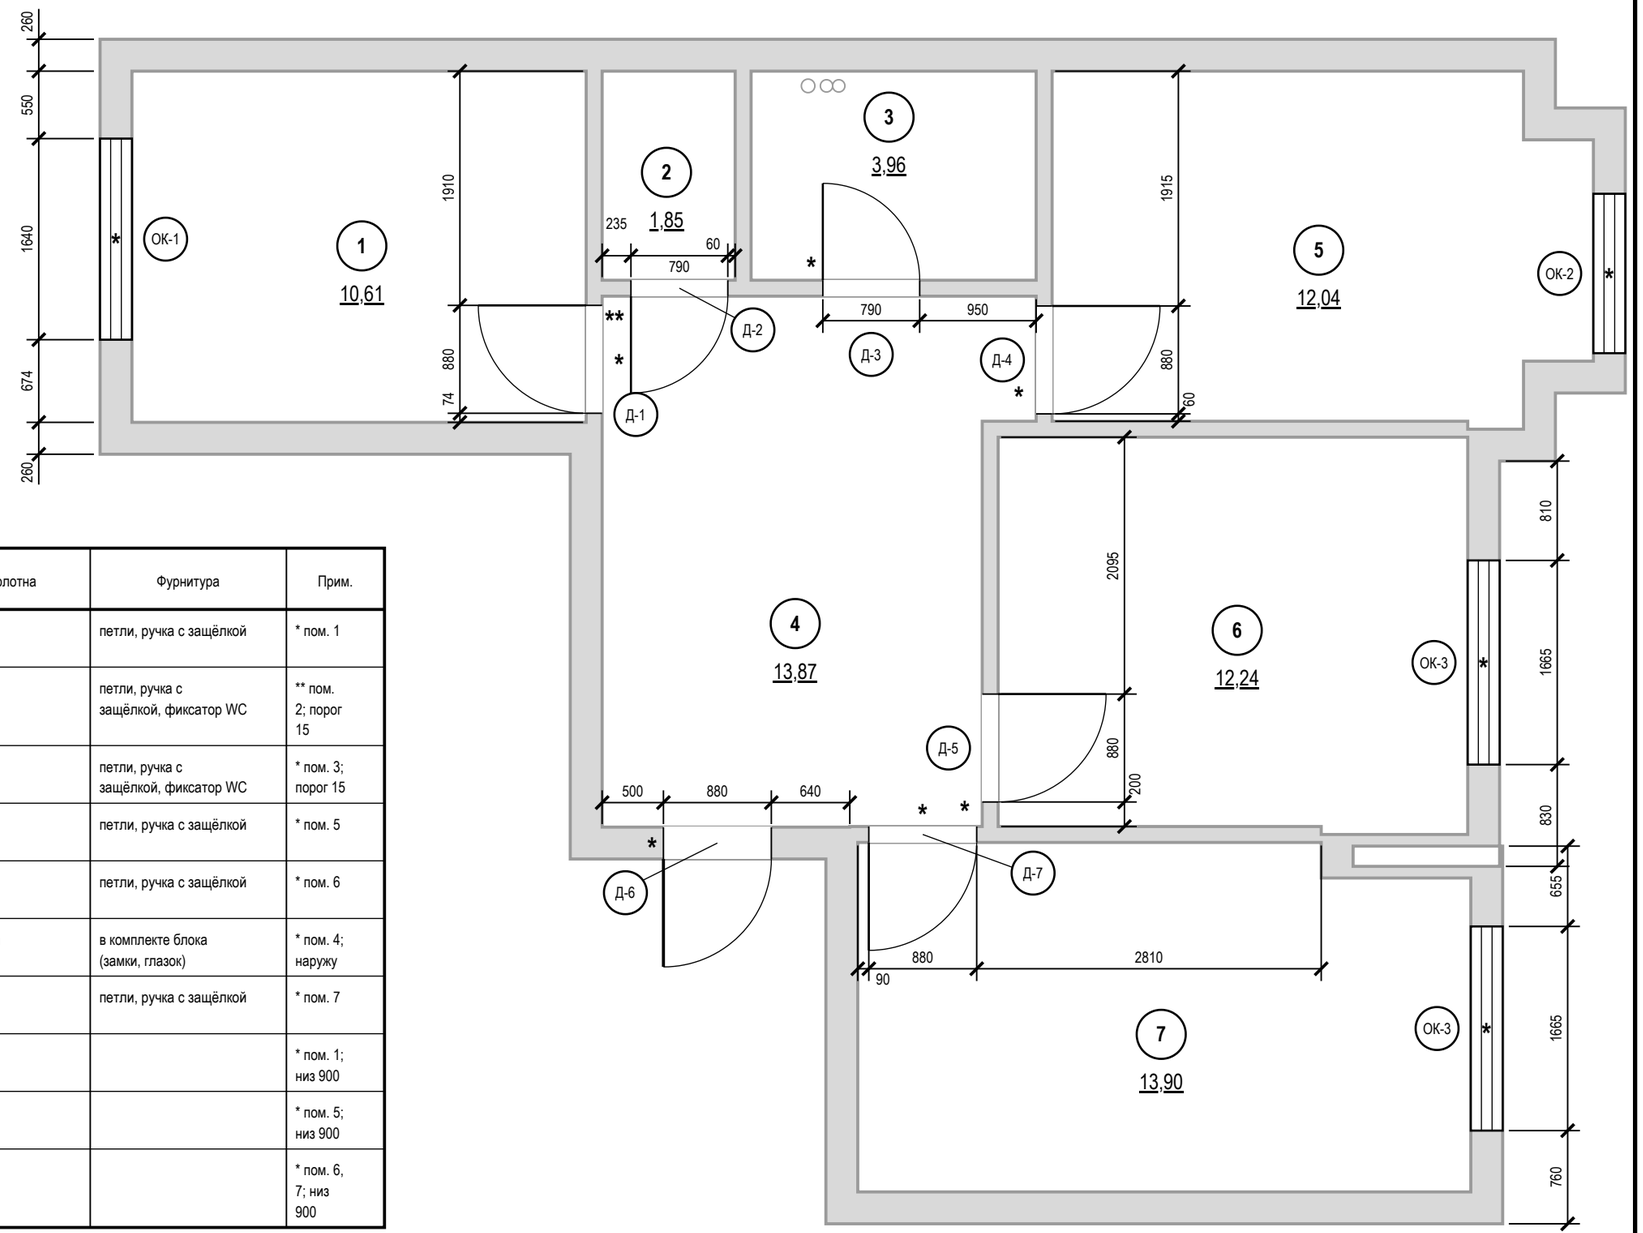

Ведомость заполнения проёмов

Марка	Наименование, обозначение	Проём ш×в, мм	Полотно (расч.)	Кол.	Откр.	Отделка полотна	Фурнитура	Прим.
Д-1	Блок дверной внутренний, ГОСТ 475-2016	880×2100	800×2000	1	Л		петли, ручка с защёлкой	* пом. 1
Д-2	Блок дверной внутренний, ГОСТ 475-2016	790×2100	700×2000	1	Л		петли, ручка с защёлкой, фиксатор WC	** пом. 2; порог 15
Д-3	Блок дверной внутренний, ГОСТ 475-2016	790×2100	700×2000	1	П		петли, ручка с защёлкой, фиксатор WC	* пом. 3; порог 15
Д-4	Блок дверной внутренний, ГОСТ 475-2016	880×2100	800×2000	1	П		петли, ручка с защёлкой	* пом. 5
Д-5	Блок дверной внутренний, ГОСТ 475-2016	880×2100	800×2000	1	П		петли, ручка с защёлкой	* пом. 6
Д-6	Блок дверной входной, ГОСТ 31173-2016	880×2100	блок задать	1	Л	в комплекте блока	в комплекте блока (замки, глазок)	* пом. 4; наружу
Д-7	Блок дверной внутренний, ГОСТ 475-2016	880×2100	800×2000	1	Л		петли, ручка с защёлкой	* пом. 7
ОК-1	Блок оконный, ГОСТ 23166-2021	1640×1500		1				* пом. 1; низ 900
ОК-2	Блок оконный, ГОСТ 23166-2021	1300×1500		1				* пом. 5; низ 900
ОК-3	Блок оконный, ГОСТ 23166-2021	1665×1500		2				* пом. 6, 7; низ 900

Примечания

1. Размеры проёмов и привязки — в миллиметрах от чистых граней стен до отделки; привязка — от угла того помещения, со стороны которого стоит размер. Размер проёма — ширина × высота от чистого пола 0,000. Размеры на плане — проёмов, не полотен: полотно — в ведомости, коробка — по системе.
2. Марки в кружках — типы заполнения проёмов (ГОСТ 21.501-2018, п. 5.3.2); одна марка — один типоразмер; количество сверено с планом.
3. Открывание: Л — петли слева, П — справа, если смотреть со стороны, куда открывается полотно (на себя).
4. Дверные блоки обычного монтажа (Д-1…Д-5, Д-7) заказывать после чистовой стяжки и штукатурки, проёмы перемерить; монтажный зазор коробки 10–15 мм на сторону, откос от угла помещения до коробки — не менее 50 мм.
5. Полотно «расч.» — по проёму с запасом по каталогам, заказ — по таблице проёмов модели; Д-1…Д-5, Д-7: проём 2100, а под полотно 2000 по каталогам нужен 2040–2080, под 2100 — 2140–2180: высоту проёма — по модели; Д-6: входной блок по ГОСТ 31173-2016 — задать при выборе блока.
6. Д-2, Д-6: дуга наружу — по плану заказчика, не проверено; блок оставить или заменить — не решено (К-1).
7. Знак «*» у проёма — допущение: положение проёма не замерено (окно пом. 1, стена Г; дверь пом. 1, стена Б; дверь пом. 3, стена В; дверь пом. 4, стена В; окно пом. 5, стена Б; дверь пом. 5, стена Г; и ещё 4); размер напечатан как принятый; в ведомости — знак «*» в графе «Прим.». Реестр: листы 5–7, вопросы К-1, К-28.
8. Экспликация помещений — лист 15; в марках помещений — номер и площадь, м².

1000 мм · печать 1:1

Допущения и предложения на листе. Знак «*» принято (замерить): Ст К1-1, Ст В1-2, Ст Т3-3. Знак «**» предложено (согласовать). См. лист открытых вопросов (листы 5–7).

Изм.	Кол.уч	Лист	№ док.	Подп.	Дата
Разраб.		Кырлан А.С.			04.11.26
Пров.					
ГИП					
Н. контр.					
Утв.					

ГД-2026-020-АИ

Квартира 68 м², элитный модерн

Общая площадь 68,47* м² · * размеры приняты, не замерены (реестр — л. 5–7, К-1)

Дизайн-проект интерьера

Стадия	Лист	Листов
РП	17	105

План дверей и ведомость заполнения проёмов

М 1:50

Кырлан Александр Сергеевич

выпуск 04.11.2026 № 8be4ef4c81 · стр. 18 из 117

02

Планировочное решение

Кырлан Александр Сергеевич

выпуск 04.11.2026 № 8be4ef4c81 · стр. 19 из 117

Концепция интерьера


Современный (контемпорари) · схема комплементарная · 60/30/10 · материалы, образы и зонирование

ПРЕДВАРИТЕЛЬНО · не для производства работ · открыто пунктов: 25 (реестр — л. 5–7)


Идея

Современный (контемпорари) + Тихая роскошь (quiet luxury) по брифу сайта для Тест (обкатка): 2 чел.. Стены Pointing, дерево — дуб натуральный, у каждой комнаты свой акцент и своя картина; кухня линейная с навесными шкафами. Обязательно: Стиль модерн, современный премиальный, премиальные материалы. Бюджет: Элитный проект, премиум. Стиль — современный (контемпорари): актуальность, комфорт, мягкая геометрия, контраст фактур, открытость, уверенность. Современный (контемпорари) + Тихая роскошь (quiet luxury): стены Pointing (тёплый белый, известковый шов), потолки Calla (кремовый универсальный белый); второй план — Shaded White, S 2010-Y30R, Pumice; акценты по комнатам — S 7010-Y50R, S 6020-G70Y, Bancha, Mouse's Back (K-7). Цветовая схема — комплементарная, пропорция 60/30/10: база на стенах и потолках, вторичный цвет — в текстиле и мягкой мебели, акцент — точечно.

Мудборд: материалы и фактуры

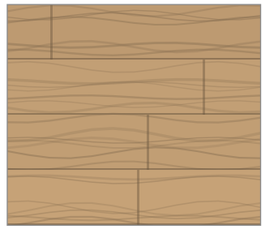

Инженерная доска, дуб натуральный
пол

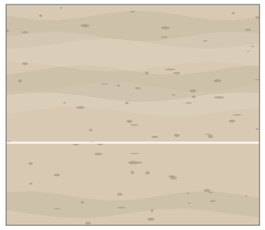

Керамогранит ректифицированный под травертин
пол



Calla · Tikkurila G503
потолок



Pointing · Farrow & Ball No. 2003
стены, плинтус



Hague Blue — глубокий сине-зелёный · Farrow & Ball No. 30
акцент (стена B)




Stiffkey Blue — чернильный синий · Farrow & Ball No. 281
акцент (стена B)



Eating Room Red — брусничный красный · Farrow & Ball No. 43
акцент (стена A)



Calke Green — традиционный шалфей · Farrow & Ball No. 34
акцент (стена B)

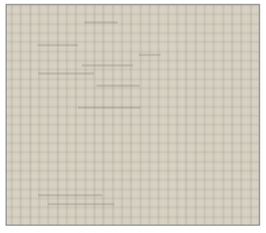

Лён, Farrow & Ball No. 201
портьеры в пол на потолочном карнизе, рулонная штора в проёме окна

Палитра 60/30/10



60 % база — Tikkurila G503 Calla, LRV 89; Farrow & Ball No. 2003 Pointing, LRV 86; Tikkurila V503 Winter, LRV 86

30 % вторичный — Farrow & Ball No. 201 Shaded White, LRV 63; NCS S 2010-Y30R, LRV 60; Tikkurila H487 Pumice, LRV 57

10 % акцент — NCS S 7010-Y50R, LRV 8; NCS S 6020-G70Y, LRV 12; Farrow & Ball No. 298 Bancha, LRV 14; Farrow & Ball No. 40 Mouse's Back, LRV 26; Farrow & Ball No. 30 Hague Blue — глубокий сине-зелёный, LRV 7; Farrow & Ball No.

Допущения и предложения на листе. См. лист открытых вопросов (листы 5–7).

Примечания

1. Коды цвета — по веерам производителей (колерная карта, лист 56); перед закупкой краски — выкрас на стене объекта под дневным светом и лампами проекта.
2. Материалы — по ведомости отделки (лист 54); мебель, текстиль и декор — по спецификации (лист 20). Образцы доски, керамогранита и тканей утвердить до заказа.
3. Фактуры на листе условные, цвет передан по HEX-значениям производителей: при печати возможны отклонения, решение — только по физическому образцу.

Функциональное зонирование (М 1:200)



дневная зона: гостиная, кухня, столовая
ночная зона: спальни
мокрая зона: санузлы
вход и коммуникации
(1) номер помещения (лист 19)

Образы помещений

6. Гостиная 12,24 м²



стены Farrow & Ball No. 2003; акцент No. 43 на стене A
пол — доска, дуб натуральный
текстиль: портьеры в пол на потолочном карнизе No. 201, тюль лён натуральный в пол G503, ковёр фактурный шерсть с джутом No. 201

5. Кухня-столовая 12,04 м²



стены Farrow & Ball No. 2003; акцент No. 281 на стене B
пол — доска, дуб натуральный
текстиль: рулонная штора в проёме окна No. 201
декор: ваза с живыми, часы настенные Ø300
свет 2700 K

7. Спальня 13,90 м²



стены Farrow & Ball No. 2003; акцент No. 34 на стене B
пол — доска, дуб натуральный
текстиль: портьеры в пол на потолочном карнизе No. 201, тюль лён натуральный в пол G503, ковёр фактурный шерсть с джутом No. 201

1. Кабинет 10,61 м²



стены Farrow & Ball No. 2003; акцент No. 30 на стене B
пол — доска, дуб натуральный
текстиль: портьеры в пол на потолочном карнизе No. 201, тюль лён натуральный в пол G503
свет 2700 K

4. Прихожая 13,87 м²



стены Farrow & Ball No. 2003
пол — керамогранит под травертин, матовый
декор: зеркало над скамьёй
свет 2700 K

3. Ванная 3,96 м²



стены — керамогранит под травертин
пол — керамогранит под травертин, матовый
декор: зеркало над умывальником
свет 2700 K

2. Санузел 1,85 м²



стены — керамогранит под травертин
пол — керамогранит под травертин, матовый
декор: зеркало над умывальником
свет 2700 K

Материалы и отделка



Инженерная доска, дуб натуральный
масло, 1-полосная, 14/4 мм
пол — пом. 1, 5, 6, 7



Керамогранит ректифицированный под травертин
матовый; 600×600, 600×1200
пол — пом. 2, 3, 4



Керамогранит под травертин
матовый; 600×1200, 1200×600
стены, фартук — пом. 2, 3, 5



Farrow & Ball No. 2003 Pointing, LRV 86
Farrow & Ball Modern Emulsion, матовая
стены, плинтус — пом. 1, 4, 5, 6, 7



Tikkurila G503 Calla, LRV 89
Tikkurila Euro Power 7, глубокоматовая
потолок — пом. 1, 2, 3, 4, 5, 6, 7



Farrow & Ball No. 30 Hague Blue — глубокий сине-зелёный, LRV 7
акцентная стена
акцент (стена B) — пом. 1



Farrow & Ball No. 281 Stiffkey Blue — чернильный синий, LRV 10.1
акцентная стена
акцент (стена B) — пом. 5



Farrow & Ball No. 43 Eating Room Red — брусничный красный, LRV 11.8
акцентная стена
акцент (стена A) — пом. 6



Farrow & Ball No. 34 Calke Green — традиционный шалфей, LRV 22
акцентная стена
акцент (стена B) — пом. 7

Текстиль и металл



Лён, Farrow & Ball No. 201
портьеры в пол на потолочном карнизе, рулонная штора в проёме окна



Вуаль, Tikkurila G503
тюль лён натуральный в пол



Шерсть, Farrow & Ball No. 201
портьеры в пол на потолочном карнизе, ковёр фактурный шерсть с джутом



Лён, NCS S 2010-Y30R
подушки бархат и жаккард: бордо



Бархат, Farrow & Ball No. 298
подушки бархат и жаккард: бордо



Шерсть, Farrow & Ball No. 298
плед шерсть с бахромой



Букле, NCS S 2010-Y30R
подушки бархат и жаккард: бордо



Лён, Farrow & Ball No. 40
подушки бархат и жаккард: бордо



Шерсть, Farrow & Ball No. 40
плед шерсть с бахромой

Чего избегаем

1) Смешение трёх и более металлов в одной комнате
2) Мебель из каталога всё сразу одной коллекции — теряется слоистость
3) Тренды без базы: весь интерьер на букле и арках к 2027 устареет
4) Глянцевый натяжной потолок и хромированные хай-тек детали 2000-х
5) Перегрузка акцентами разного цвета (синий + зелёный + терракота в одной комнате)
6) Холодный свет 4000 K в жилых зонах

Изм.	Кол.уч	Лист	№ док.	Подп.	Дата
Разраб.		Кырлан А.С.			04.11.26
Пров.					
ГИП					
Н. контр.					
Утв.					

ГД-2026-020-АИ

Квартира 68 м², элитный модерн

Общая площадь 68,47* м² · * размеры приняты, не замерены (реестр — л. 5–7, К-1)

Дизайн-проект интерьера	Стадия	Лист	Листов
	РП	18	105

Концепция интерьера
М б/м


Кырлан Александр Сергеевич

выпуск 04.11.2026 № 8be4ef4c81 · стр. 20 из 117

План расстановки мебели

Мебель и оборудование · размеры в мм от чистовых стен · марки — по ведомости

ПРЕДВАРИТЕЛЬНО · не для производства работ · открыто пунктов: 25 (реестр — л. 5–7)

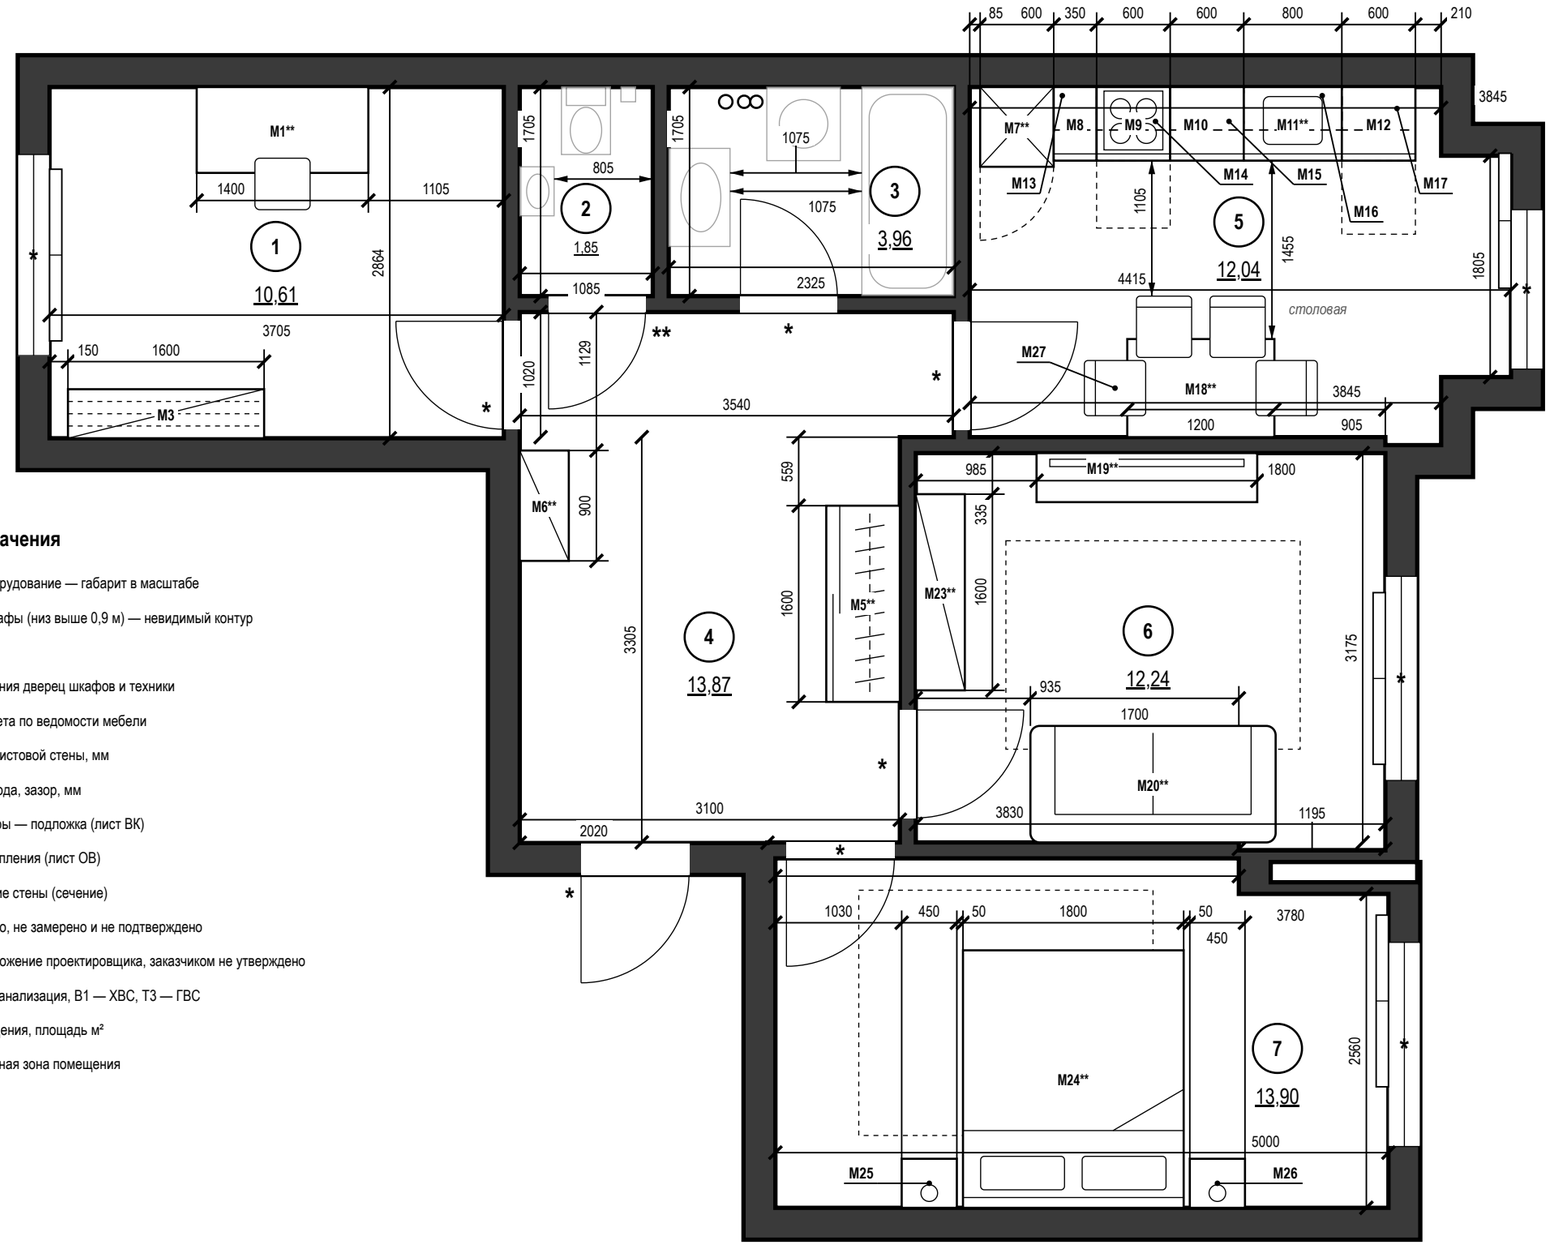

Условные обозначения

- мебель и оборудование — габарит в масштабе
- навесные шкафы (низ выше 0,9 м) — невидимый контур
- ковёр
- зона открывания дверец шкафов и техники
- **К1** — марка предмета по ведомости мебели
- привязка от чистовой стены, мм
- ширина прохода, зазор, мм
- сантехприборы — подложка (лист ВК)
- радиатор отопления (лист ОВ)
- существующие стены (сечение)
- * — «*» — принято, не замерено и не подтверждено
- ** — «**» — предложение проектировщика, заказчиком не утверждено
- стояк: К1 — канализация, В1 — ХВС, Т3 — ГВС
- 1 — номер помещения, площадь м²
- *зона* — функциональная зона помещения

Экспликация помещений

лист 15 · на плане — номера в марках

Ведомость мебели и оборудования

Марка	Наименование	Ш×Г×В, мм	Пом.	Кол.
M1**	Стол письменный 1400×700	1400×700×750	1	1
M3	Стеллаж для книг 1600×400	1600×400×2200	1	1
M5**	Шкаф-купе 1600×600 до потолка	1600×600×2450	4	1
M6**	Скамья-обувница 900×400	900×400×450	4	1
M7**	Колонна с холодильником встроенным;	600×650×2200	5	1
M8	Модуль узкий	350×600×900	5	1
M9	Модуль с варочной панелью	600×600×900	5	1
M10	Модуль с ящиками	600×600×900	5	1
M11**	Модуль под мойку; столешница	800×600×900	5	1
M12	Посудомоечная машина встроенная 600	600×600×900	5	1
M18**	Стол обеденный 1200×800	1200×800×750	5	1
M13	Навесной шкаф	350×350×900	5	1
M14	Вытяжка встроенная в навесной шкаф	600×350×800	5	1
M15	Навесной шкаф	600×350×900	5	1
M16	Навесной шкаф с сушкой	800×350×900	5	1
M17	Навесной шкаф	600×350×900	5	1
M19**	ТВ-стена в стеновых панелях	1800×400×450	6	1
M20**	Диван полукруглый модульный 2000×950	2000×950×850	6	1
M23**	Консоль 1600×400 красного дерева	1600×400×750	6	1
M24**	Кровать 1800×2100	1800×2100×900	7	1
M25	Тумба прикроватная левая	450×400×500	7	1
M26	Тумба прикроватная правая	450×400×500	7	1
M27	Стул обеденный к столу M18**	450×500×820	5	4

Ш — вдоль стены (изголовья), Г — от стены (длина кровати)

Материалы, модели, допуск замены — лист 20

Допущения и предложения на листе. Основа листа: планировка по обводу плана заказчика, не замерена (К-1); высота до плиты 2650 мм от чистого пола — решение автора (ИЗ-1); отметки плана потолков сдвинуты на -95 мм (+2.745 плана = низ плиты), не замерено (К-2); толщины стен приняты: наружные 260 мм, перегородки 130 мм (К-1); положение стен и проёмов — по брифу без обмера и плана БТИ (К-1); разрешённая мощность 10 кВт принята, ТУ не переданы (К-6); вентканалы приняты, в брифе не заданы (К-5); тип дома, перекрытие и несущие стены не известны — документов нет (К-3); плита электрическая — принята, в брифе не указано (К-6); система заземления TN-C-S принята, ТУ не переданы (К-6); число жильцов 2 принято, в брифе не указано (К-9); подрайон климата не задан — принят не северный (жилые от 2,5 м) (К-26). Знак «*» — принято, не замерено (замерить): К-4: Ст К1-1, Ст В1-2, Ст Т3-3. Знак «**» — предложено, не утверждено (согласовать): М6; ИЗ-2, К-7: М24. См. лист открытых вопросов (лист 5, записи К-1, К-3–К-7, К-9; лист 6, запись К-26; лист 7, запись ИЗ-2).

Примечания

1. Размеры — в мм от чистовых поверхностей стен, размеры помещений — в свету, привязки — от стен, углов помещения и соседних предметов, проходы и зазоры — стрелками; розетки и выводы под мебель — лист 23, выключатели — лист 25, сантехприборы лист 34.
2. Общие указания к расстановке (чистовой слой, контрольный обмер, зазоры встроенной мебели, замена покупной) — примечания к спецификации, лист 20.
3. Стулья обеденной группы (M27 — 4 шт.) показаны в рабочем положении, задвинутыми под столешницу на 150 мм.

1000 мм · печать 1:1

Изм.	Кол.уч	Лист	№ док.	Подп.	Дата
Разраб.		Кырлан А.С.			04.11.26
Пров.					
ГИП					
Н. контр.					
Утв.					

ГД-2026-020-АИ

Квартира 68 м², элитный модерн

Общая площадь 68,47* м² · * размеры приняты, не замерены (реестр — л. 5–7, К-1)

Дизайн-проект интерьера

Стадия	Лист	Листов
РП	19	105

План расстановки мебели

М 1:50

Кырлан Александр Сергеевич

выпуск 04.11.2026 № 8be4ef4c81 · стр. 21 из 117

Спецификация мебели и оборудования

ПРЕДВАРИТЕЛЬНО · не для производства работ · открыто пунктов: 25 (реестр — л. 5–7)

Форма 1 ГОСТ 21.110-2013 · позиции мебели — по плану расстановки

Поз.	Наименование и техническая характеристика	Тип, марка, обозначение документа, опросного листа	Код продукции	Поставщик	Ед. измерения	Кол.	Масса 1 ед., кг	Примечание
	Мебель встроенная и корпусная (изготовление по чертежам мебельщика)							
M5**	Шкаф-купе 1600×600 до потолка: филёнчатые фасады эмаль пыльно-синяя и бронзовое зеркало, латунные ручки; корпус ЛДСП 16 мм; фасады — МДФ, шпон / эмаль 18 мм; вставка — зеркало серебро 4 мм на безопасной плёнке, в профиле двери; Ш×Г×В 1600×600×2450 мм			изготовление на заказ	шт.	1		пом. 4
M7**	Колонна с холодильником встроенным; фасады — МДФ: шпон американского ореха (нижние модули) и эмаль пыльно-синяя с узкой филёнкой (колонны), латунные ручки-скобы; фурнитура — латунь браированная; корпус ЛДСП 16 мм; фасады МДФ: шпон американского ореха (нижние модули) и эмаль пыльно-синяя с узкой филёнкой (колонны), латунные ручки-скобы 18 мм; Ш×Г×В 600×650×2200 мм			изготовление на заказ	шт.	1		пом. 5; крепление к стене
M8	Модуль узкий с выдвижными ящиками 350; корпус ЛДСП 16 мм; фасады — МДФ: шпон американского ореха (нижние модули) и эмаль пыльно-синяя с узкой филёнкой (колонны), латунные ручки-скобы 18 мм; Ш×Г×В 350×600×900 мм			изготовление на заказ	шт.	1		пом. 5
M9	Модуль с варочной панелью и духовым шкафом; корпус ЛДСП 16 мм; фасады — МДФ: шпон американского ореха (нижние модули) и эмаль пыльно-синяя с узкой филёнкой (колонны), латунные ручки-скобы 18 мм; Ш×Г×В 600×600×900 мм			изготовление на заказ	шт.	1		пом. 5
M10	Модуль с ящиками; корпус ЛДСП 16 мм; фасады — МДФ: шпон американского ореха (нижние модули) и эмаль пыльно-синяя с узкой филёнкой (колонны), латунные ручки-скобы 18 мм; Ш×Г×В 600×600×900 мм			изготовление на заказ	шт.	1		пом. 5
M11**	Модуль под мойку; столешница — мрамор с яркой прожилкой (типа Calacatta Viola), 20 мм, фартук одним слэбом; корпус ЛДСП 16 мм; фасады — МДФ: шпон американского ореха (нижние модули) и эмаль пыльно-синяя с узкой филёнкой (колонны), латунные ручки-скобы 18 мм; Ш×Г×В 800×600×900 мм			изготовление на заказ	шт.	1		пом. 5
M12	Модуль под встраиваемую ПММ 60; без корпуса (ниша между соседними модулями); фасад на дверь машины — МДФ: шпон американского ореха (нижние модули) и эмаль пыльно-синяя с узкой филёнкой (колонны), латунные ручки-скобы 18 мм; цоколь; Ш×Г×В 600×600×900 мм			изготовление на заказ	шт.	1		пом. 5
M13	Навесной шкаф; корпус ЛДСП 16 мм; фасады — МДФ, эмаль пыльно-синяя, филёнка, латунные ручки 18 мм; Ш×Г×В 350×350×900 мм			изготовление на заказ	шт.	1		пом. 5
M14	Вытяжка встроенная в навесной шкаф, рециркуляция до обмера вентканала; корпус ЛДСП 16 мм; фасады — МДФ, эмаль пыльно-синяя, филёнка, латунные ручки 18 мм; Ш×Г×В 600×350×800 мм			изготовление на заказ	шт.	1		пом. 5
M15	Навесной шкаф; корпус ЛДСП 16 мм; фасады — МДФ, эмаль пыльно-синяя, филёнка, латунные ручки 18 мм; Ш×Г×В 600×350×900 мм			изготовление на заказ	шт.	1		пом. 5
M16	Навесной шкаф с сушкой; корпус ЛДСП 16 мм; фасады — МДФ, эмаль пыльно-синяя, филёнка, латунные ручки 18 мм; Ш×Г×В 800×350×900 мм			изготовление на заказ	шт.	1		пом. 5
M17	Навесной шкаф; корпус ЛДСП 16 мм; фасады — МДФ, эмаль пыльно-синяя, филёнка, латунные ручки 18 мм; Ш×Г×В 600×350×900 мм			изготовление на заказ	шт.	1		пом. 5
	Мебель покупная							
M1**	Стол письменный 1400×700, шпон ореха на изогнутых опорах, кожаная вставка, латунная фурнитура; дерево — дуб натуральный, металл — чёрный матовый; Ш×Г×В 1400×700×750 мм			аналог по характеристикам	шт.	1		пом. 1; замена ≤ габарита
M3	Стеллаж для книг 1600×400, каркас — чёрная сталь, полки — дуб натуральный; каркас — чёрная сталь, полки — массив дуб натуральный; Ш×Г×В 1600×400×2200 мм			аналог по характеристикам	шт.	1		пом. 1; крепление к стене; замена ≤ габарита
M6**	Скамья-обувница 900×400, дуб натуральный, с сушилкой для обуви (предложение); дерево — дуб натуральный; Ш×Г×В 900×400×450 мм			аналог по характеристикам	шт.	1		пом. 4; замена ≤ габарита
M18**	Стол обеденный 1200×800 на скульптурной круглой опоре, мрамор с яркой прожилкой; стулья бархат бордо на латунных ножках, 4 шт.; дерево — дуб натуральный; Ш×Г×В 1200×800×750 мм			аналог по характеристикам	шт.	1		пом. 5; замена ≤ габарита
M27	Стул обеденный к столу M18**; обивка — ткань, цвет Farrow & Ball No. 201; каркас — дуб натуральный; Ш×Г×В 450×500×820 мм			аналог по характеристикам	шт.	4		пом. 5; замена ≤ габарита
M19**	ТВ-стена в стеновых панелях с молдингами и арочной нишей с подсветкой; тумба 1800×400 шпон ореха, мраморная столешница, ТВ 55" дерево — дуб натуральный; Ш×Г×В 1800×400×450 мм			аналог по характеристикам	шт.	1		пом. 6; замена ≤ габарита

Примечания

1. Позиции мебели совпадают с марками на плане расстановки (лист 19); размеры Ш×Г×В — Ш вдоль стены, Г от стены.
2. Размеры и привязки плана расстановки — в мм от чистовых поверхностей стен: слой штукатурки 20 мм по блоку и 5 мм шпаклёвки по ГКЛ учтён; привязки — от стен и углов помещения, а не от другой мебели.
3. План расстановки не является документацией для изготовления мебели. Встроенная и корпусная мебель изготавливается по чертежам мебельщика после контрольного обмера (после штукатурки); «стена в стену» — с зазором 10 мм с каждой стороны или с компенсаторами; графы «Тип, марка» и «Код продукции» для неё не заполняются (ГОСТ 21.110-2013).
4. Покупные изделия — аналог по характеристикам: заменять только на изделия не больше указанного габарита и того же материала и цвета.
5. Материал и цвет, не указанные в данных изделия, приняты по концепции (лист 18): тон дерева — по полу, обивка — по вторичному цвету палитры; образцы согласовать до заказа.
6. Масса 1 ед. для изделий до 25 кг не указывается. Техника — по монтажным схемам изготовителя; выводы — по листам ЭОМ и ВК.

Допущения и предложения на листе. Основа листа: планировка по обводу плана заказчика, не замерена (К-1); высота до плиты 2650 мм от чистого пола — решение автора (ИЗ-1); отметки плана потолков сдвинуты на -95 мм (+2.745 плана = низ плиты), не замерено (К-2); толщины стен приняты: наружные 260 мм, перегородки 130 мм (К-1); положение стен и проёмов — по брифу без обмера и плана БТИ (К-1); разрешённая мощность 10 кВт принята, ТУ не переданы (К-6); вентканалы приняты, в брифе не заданы (К-5); тип дома, перекрытие и несущие стены не известны — документов нет (К-3); плита электрическая — принята, в брифе не указано (К-6); система заземления TN-C-S принята, ТУ не переданы (К-6); число жильцов 2 принято, в брифе не указано (К-9); подрайон климата не задан — принят не северный (жилые от 2,5 м) (К-26). Знак «**» — предложение проектировщика, заказчиком не утверждено (согласовать с заказчиком): M6 — сушилка для обуви под скамьёй — предложение по умолчанию (комфорт), заказчик может снять; питание — розетка «уборка, сушилка обуви». См. лист открытых вопросов (лист 5, записи К-1, К-3, К-5–К-7, К-9; лист 6, запись К-26).

Изм.	Кол.уч	Лист	№ док.	Подп.	Дата
Разраб.		Кырлан А.С.			04.11.26
Пров.					
ГИП					
Н. контр.					
Утв.					

ГД-2026-020-АИ

Квартира 68 м², элитный модерн

Общая площадь 68,47* м² · * размеры приняты, не замерены (реестр — л. 5–7, К-1)

Дизайн-проект интерьера	Стадия	Лист	Листов
	РП	20	105

Спецификация мебели и оборудования

М б/м

Кырлан Александр Сергеевич

выпуск 04.11.2026 № 8be4ef4c81 · стр. 22 из 117

Спецификация мебели и оборудования (продолжение)

ПРЕДВАРИТЕЛЬНО · не для производства работ · открыто пунктов: 25 (реестр — л. 5–7)

Форма 1 ГОСТ 21.110-2013 · позиции мебели — по плану расстановки

Поз.	Наименование и техническая характеристика	Тип, марка, обозначение документа, опросного листа	Код продукции	Поставщик	Ед. измерения	Кол.	Масса 1 ед., кг	Примечание
М20**	Диван полукруглый модульный 2000×950, глубокая посадка, бархат бордо (оксблад), латунный цоколь; обивка букле; Ш×Г×В 2000×950×850 мм			аналог по характеристикам	шт.	1		пом. 6; замена ≤ габарита
М23**	Консоль 1600×400 красного дерева (шпон сапеле) на гнутых ножках, мраморная столешница с яркой прожилкой; пуф бархат; дерево — дуб натуральный; Ш×Г×В 1600×400×750 мм			аналог по характеристикам	шт.	1		пом. 6; крепление к стене; замена ≤ габарита
М24**	Кровать 1800×2100 с панельным изголовьем во всю стену: стёганый бархат шалфей, латунный кант; обивка кожа натуральная, дерево — дуб натуральный; Ш×Г×В 1800×2100×900 мм			аналог по характеристикам	шт.	1		пом. 7; замена ≤ габарита
М25	Тумба прикроватная левая, дуб натуральный; дерево — дуб натуральный; Ш×Г×В 450×400×500 мм			аналог по характеристикам	шт.	1		пом. 7; замена ≤ габарита
М26	Тумба прикроватная правая, дуб натуральный; дерево — дуб натуральный; Ш×Г×В 450×400×500 мм			аналог по характеристикам	шт.	1		пом. 7; замена ≤ габарита
	Техника встраиваемая и бытовая (покупные изделия), светильники под розетки							
	Стиральная машина, место по листу ВК (П16**); Ш×Г 600×600 мм	аналог по характеристикам: фронтальная загрузка, в плане 600 × 600 мм (ширина × глубина), по листу ВК		по выбору заказчика до изготовления мебели	шт.	1		пом. 3; по схеме изготовителя
	Сушильная машина встраиваемая, у М6**	аналог по характеристикам: тип загрузки — по листу ВК, по листу ВК		по выбору заказчика до изготовления мебели	шт.	1		пом. 4; по схеме изготовителя
	Холодильник встраиваемый, в модуле М7**	аналог по характеристикам: полновстраиваемый под фасад, ниша 1780 × 560 × 550 мм, вентиляция решётка в цоколе, выход сверху		по выбору заказчика до изготовления мебели	шт.	1		пом. 5; по схеме изготовителя
	Духовой шкаф встраиваемый, в модуле М9	аналог по характеристикам: 60 см, лицевая панель 595 мм, ниша 560 × 600, глубина ≥ 550 мм, вентиляция за прибором		по выбору заказчика до изготовления мебели	шт.	1		пом. 5; по схеме изготовителя
	Варочная панель встраиваемая, индукционная, в модуле М9	аналог по характеристикам: индукционная 60 см, вырез 560 × 490 мм по шаблону модели		по выбору заказчика до изготовления мебели	шт.	1		пом. 5; по схеме изготовителя
	Посудомоечная машина встраиваемая, в модуле М12; ниша 600 мм	аналог по характеристикам: полновстраиваемая 60 см под фасад, ниша 600 × 862 мм, навеска фасада в комплекте		по выбору заказчика до изготовления мебели	шт.	1		пом. 5; по схеме изготовителя
	Вытяжка встраиваемая, в модуле М14	аналог по характеристикам: производительность — по расчёту ОВ, шум ≤ 55 дБ(А)		по выбору заказчика до изготовления мебели	шт.	1		пом. 5; по схеме изготовителя
	Торшер, у поз. М20**; абажур — ткань или опаловое стекло; лампа 2700 K			аналог по характеристикам	шт.	1		пом. 6; розетка Р13 (ЭОМ)
	Торшер, у поз. М20**; абажур — ткань или опаловое стекло; лампа 2700 K			аналог по характеристикам	шт.	1		пом. 6; розетка Р36 (ЭОМ)
	Торшер, у поз. М20**; абажур — ткань или опаловое стекло; лампа 2700 K			аналог по характеристикам	шт.	1		пом. 6; розетка Р37 (ЭОМ)
	Текстиль							
Т1**	Портьеры в пол на потолочном карнизе, бархат (тон по комнате); лён / хлопок / шерсть по ткани, подкладка полиэстер; цвет Farrow & Ball No. 201; карниз 2040 мм, высота 2575 мм, сборка 2			аналог по характеристикам	шт.	2		пом. 1
Т2**	Тюль лён натуральный в пол; лён / хлопок / полиэстер по ткани; цвет Tikkurila G503; карниз 2040 мм, высота 2575 мм, сборка 2,5			аналог по характеристикам	шт.	1		пом. 1
Т3	Рулонная штора в проёме окна, ткань блэкаут; полиэстер 100 %; цвет Farrow & Ball No. 201; карниз 1260 мм, высота 1460 мм			аналог по характеристикам	шт.	1		пом. 5
Т4**	Портьеры в пол на потолочном карнизе, бархат (тон по комнате); лён / хлопок / шерсть по ткани, подкладка полиэстер; цвет Farrow & Ball No. 201; карниз 2065 мм, высота 2575 мм, сборка 2			аналог по характеристикам	шт.	2		пом. 6
Т5**	Тюль лён натуральный в пол; лён / хлопок / полиэстер по ткани; цвет Tikkurila G503; карниз 2065 мм, высота 2575 мм, сборка 2,5			аналог по характеристикам	шт.	1		пом. 6

Допущения и предложения на листе

Основа листа: планировка по обводу плана заказчика, не замерена (К-1); высота до плиты 2650 мм от чистого пола — решение автора (ИЗ-1); отметки плана потолков сдвинуты на -95 мм (+2.745 плана = низ плиты), не замерено (К-2); толщины стен приняты: наружные 260 мм, перегородки 130 мм (К-1); положение стен и проёмов — по брифу без обмера и плана БТИ (К-1); разрешённая мощность 10 кВт принята, ТУ не переданы (К-6); вентканалы приняты, в брифе не заданы (К-5); тип дома, перекрытие и несущие стены не известны — документов нет (К-3); плита электрическая — принята, в брифе не указано (К-6); система заземления TN-C-S принята, ТУ не переданы (К-6); число жильцов 2 принято, в брифе не указано (К-9); подрайон климата не задан — принят не северный (жилые от 2,5 м) (К-26).

Знак «**» — предложение проектировщика, заказчиком не утверждено (согласовать с заказчиком): М6 — сушилка для обуви под скамьёй — предложение по умолчанию (комфорт), заказчик может снять; питание — розетка «уборка, сушилка обуви»; ИЗ-2, К-7: М24 — по исходному плану: прикроватные светильники 13-А / 13-Б в 2480 мм друг от друга у стены С — двуспальная кровать 1800 по центру между ними; ИЗ-3, К-7: П16 — место стиральной машины — в ванной у верхней стены, правее короба стояка; подход 1100 мм перед дверцей, выводы ХВС и К1 Ø40 за машиной; К-7: Т1, Т2, М7, М20, М23, Т4, Т5.

См. лист открытых вопросов (лист 5, записи К-1, К-3, К-5–К-7, К-9; лист 6, запись К-26; лист 7, записи ИЗ-2, ИЗ-3).

Изм.	Кол.уч	Лист	№ док.	Подп.	Дата
Разраб.		Кырлан А.С.			04.11.26
Пров.					
ГИП					
Н. контр.					
Утв.					

ГД-2026-020-АИ

Квартира 68 м², элитный модерн

Общая площадь 68,47* м² · * размеры приняты, не замерены (реестр — л. 5–7, К-1)

Дизайн-проект интерьера

Стадия	Лист	Листов
РП	21	105

Спецификация мебели и оборудования (продолжение)

М б/м

Кырлан Александр Сергеевич

выпуск 04.11.2026 № 8be4ef4c81 · стр. 23 из 117

Спецификация мебели и оборудования (продолжение)

Форма 1 ГОСТ 21.110-2013 · позиции мебели — по плану расстановки

ПРЕДВАРИТЕЛЬНО · не для производства работ · открыто пунктов: 25 (реестр — л. 5–7)

Поз.	Наименование и техническая характеристика	Тип, марка, обозначение документа, опросного листа	Код продукции	Поставщик	Ед. измерения	Кол.	Масса 1 ед., кг	Примечание
Т6**	Ковёр фактурный шерсть с джутом, тёплый терракотовый тон; шерсть / джут / хлопок по ткани; цвет Farrow & Ball No. 201; 2400×1700 мм			аналог по характеристикам	шт.	1		пом. 6; с подложкой
Т7**	Подушки бархат и жаккард: бордо, шалфей, горчица; натуральное волокно по ткани; цвет NCS S 2010-Y30R			аналог по характеристикам	шт.	3		пом. 6
Т8**	Подушки бархат и жаккард: бордо, шалфей, горчица; натуральное волокно по ткани; цвет Farrow & Ball No. 298			аналог по характеристикам	шт.	2		пом. 6
Т9**	Плед шерсть с бахромой, терракота; шерсть / хлопок по ткани; цвет Farrow & Ball No. 298			аналог по характеристикам	шт.	1		пом. 6
Т10**	Портьеры в пол на потолочном карнизе, бархат (тон по комнате); лён / хлопок / шерсть по ткани, подкладка полиэстер; цвет Farrow & Ball No. 201; карниз 2265 мм, высота 2635 мм, сборка 2			аналог по характеристикам	шт.	2		пом. 7
Т11**	Тюль лён натуральный в пол; лён / хлопок / полиэстер по ткани; цвет Tikkurila G503; карниз 2265 мм, высота 2635 мм, сборка 2,5			аналог по характеристикам	шт.	1		пом. 7
Т12**	Ковёр фактурный шерсть с джутом, тёплый терракотовый тон; шерсть / джут / хлопок по ткани; цвет Farrow & Ball No. 201; 2400×2000 мм			аналог по характеристикам	шт.	1		пом. 7; с подложкой
Т13**	Подушки бархат и жаккард: бордо, шалфей, горчица; натуральное волокно по ткани; цвет NCS S 2010-Y30R			аналог по характеристикам	шт.	3		пом. 7
Т14**	Подушки бархат и жаккард: бордо, шалфей, горчица; натуральное волокно по ткани; цвет Farrow & Ball No. 40			аналог по характеристикам	шт.	2		пом. 7
Т15**	Плед шерсть с бахромой, терракота; шерсть / хлопок по ткани; цвет Farrow & Ball No. 40			аналог по характеристикам	шт.	1		пом. 7
	Декор							
ДК9	Зеркало над умывальником, влагостойкое, с подсветкой; 400×800 мм; низ на 1200 мм от пола			аналог по характеристикам	шт.	1	5	пом. 2; крепление к стене
ДК10	Зеркало над умывальником, влагостойкое, с подсветкой; 600×800 мм; низ на 1200 мм от пола			аналог по характеристикам	шт.	1	5	пом. 3; крепление к стене
ДК1	Зеркало над скамьёй 600×1200, тонкая чёрная рама; 600×1200 мм; низ на 700 мм от пола			аналог по характеристикам	шт.	1	6	пом. 4; крепление: дюбель 2 шт.
ДК2	Ваза с живыми цветами на обеденном столе; 200×300 мм; на М18**			аналог по характеристикам	шт.	1		пом. 5
ДК3	Часы настенные Ø300; 300×300 мм; низ на 1700 мм от пола			аналог по характеристикам	шт.	1	1	пом. 5; крепление к стене
ДК4**	Крупная живопись в тонкой латунной раме над консоль низкая 1600×400: крупная абстракция широкими мазками, рама дуб натуральный; 1050×750 мм; низ на 1000 мм от пола			аналог по характеристикам	шт.	1	4	пом. 6; крепление к стене
ДК5**	Крупная живопись в тонкой латунной раме над диван 2000×950: чёрно-белая фотография города в дожде, рама — дуб натуральный; 1200×850 мм; низ на 1050 мм от пола			аналог по характеристикам	шт.	1	4	пом. 6; крепление к стене
ДК6	Оливковое дерево в кашпо Ø450; 450×450 мм			аналог по характеристикам	шт.	1		пом. 6
ДК7**	Крупная живопись в тонкой латунной раме над кровать 1400×2000: пересекающиеся дуги, рама — дуб натуральный; 900×650 мм; низ на 1100 мм от пола			аналог по характеристикам	шт.	1	4	пом. 7; крепление к стене
ДК8	Монстера в кашпо Ø450; 450×450 мм			аналог по характеристикам	шт.	1		пом. 7

Допущения и предложения на листе

Основа листа: планировка по обводу плана заказчика, не замерена (К-1); высота до плиты 2650 мм от чистого пола — решение автора (ИЗ-1); отметки плана потолков сдвинуты на -95 мм (+2.745 плана = низ плиты), не замерено (К-2); толщины стен приняты: наружные 260 мм, перегородки 130 мм (К-1); положение стен и проёмов — по брифу без обмера и плана БТИ (К-1); разрешённая мощность 10 кВт принята, ТУ не переданы (К-6); вентканалы приняты, в брифе не заданы (К-5); тип дома, перекрытие и несущие стены не известны — документов нет (К-3); плита электрическая — принята, в брифе не указано (К-6); система заземления TN-C-S принята, ТУ не переданы (К-6); число жильцов 2 принято, в брифе не указано (К-9); подрайон климата не задан — принят не северный (жилые от 2,5 м) (К-26).

Знак «**» — предложение проектировщика, заказчиком не утверждено (согласовать с заказчиком): К-7: М18, Т6, Т7, Т8, Т9, ДК4, ДК5, Т10, Т11, Т12, Т13, Т14, Т15, ДК7.

См. лист открытых вопросов (лист 5, записи К-1, К-3, К-5–К-7, К-9; лист 6, запись К-26).

Изм.	Кол.уч	Лист	№ док.	Подп.	Дата
Разраб.		Кырлан А.С.			04.11.26
Пров.					
ГИП					
Н. контр.					
Утв.					

ГД-2026-020-АИ

Квартира 68 м², элитный модерн

Общая площадь 68,47* м² · * размеры приняты, не замерены (реестр — л. 5–7, К-1)

Дизайн-проект интерьера

Стадия	Лист	Листов
РП	22	105

Спецификация мебели и оборудования (продолжение)

М б/м

Кырлан Александр Сергеевич

03

Электрооборудование


Кырлан Александр Сергеевич

выпуск 04.11.2026 · 8be4ef4c81 · стр. 25 из 117

План розеток и электровыводов

Розетки, выводы кабеля, щит · размеры в мм · высоты от чистого пола

ПРЕДВАРИТЕЛЬНО · не для производства работ · открыто пунктов: 25 (реестр — л. 5–7)

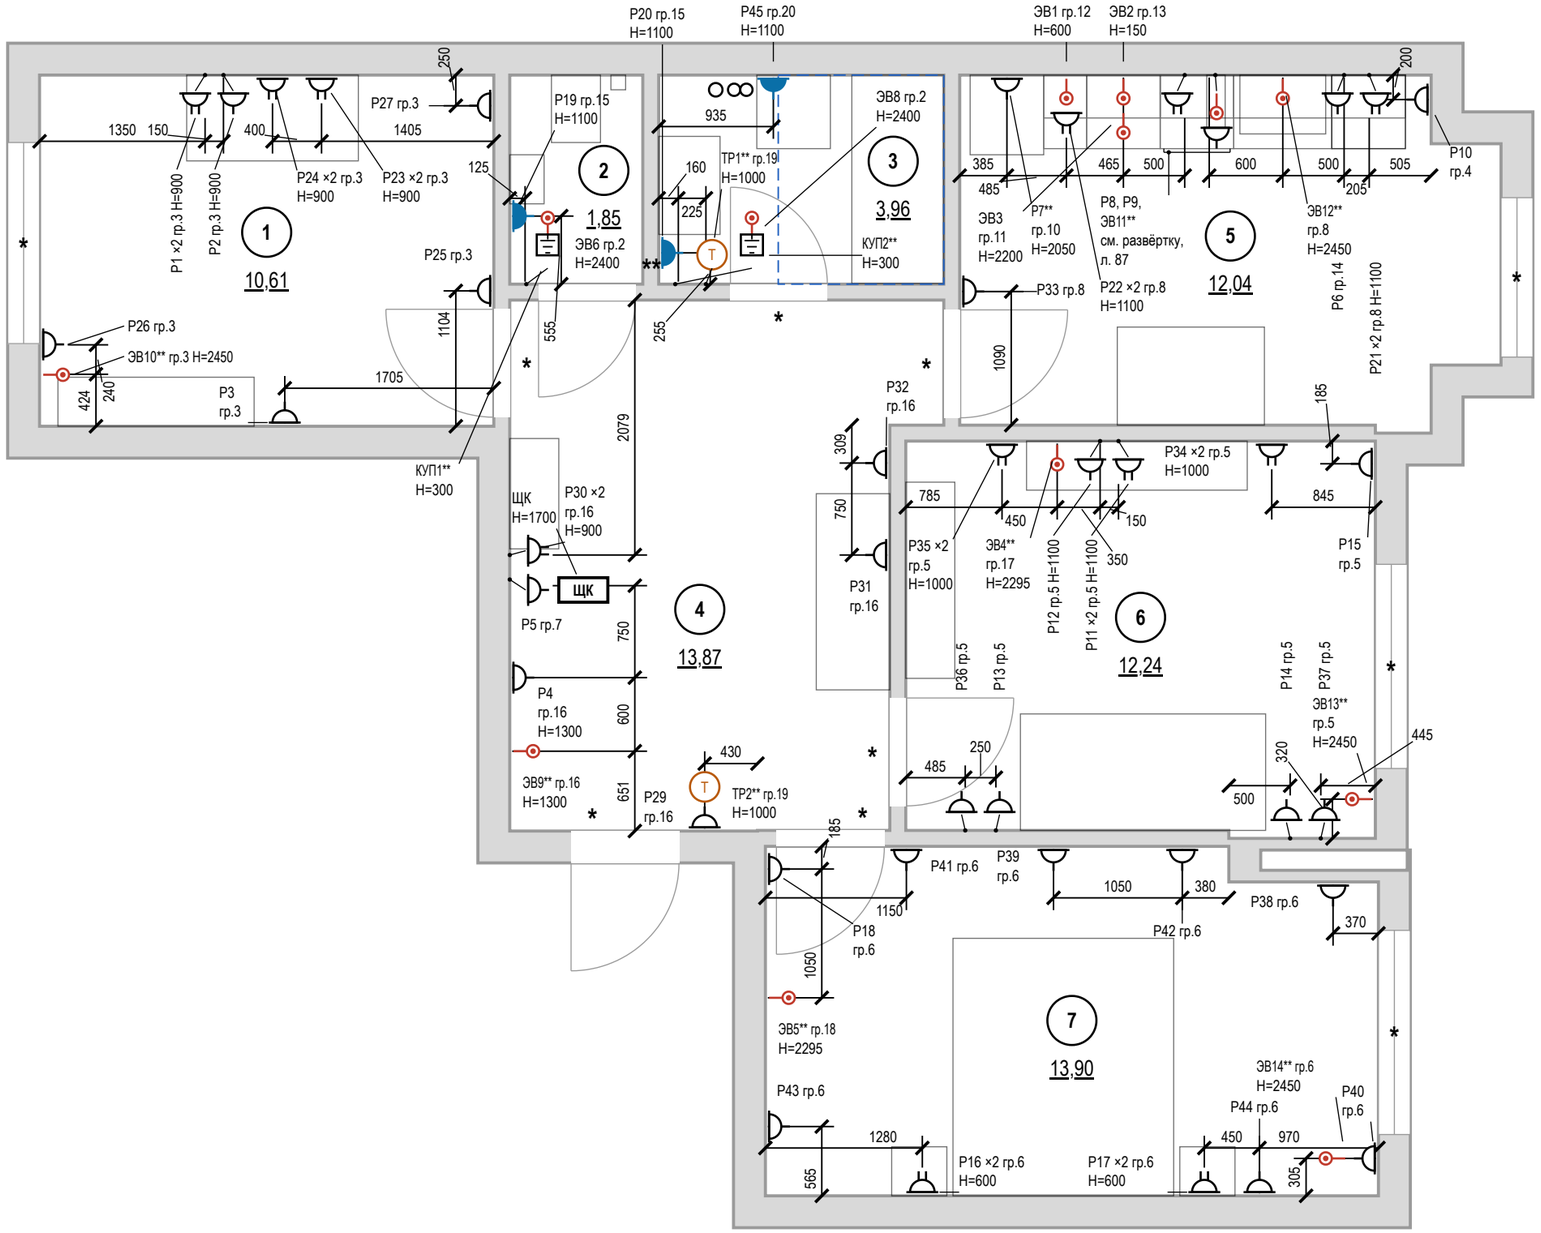

Условные обозначения

Знак	Тип изделия	H, мм	Кол., шт
	Розетка с заземлением	300	24
	То же	у знака	5
	Блок розеток с заземлением, рамка 2 поста	у знака	12
	Розетка с заземлением IP44	1100	3
	Вывод кабеля к прибору	у знака	13
КУП	КУП (уравнивание потенциалов)	300	2
T	Терморегулятор тёплого пола	1000	2
ЩК	Щит квартирный	1700	1

розетка с заземляющим контактом; у знака — марка, ×N — постов в рамке, гр. — группа щита, H — высота оси, мм

знак разведён для читаемости: точка на стене — у выноски, привязка — до неё

граница зоны 2 ванной (600 мм от ванны/поддона)

мебель и сантехприборы — подложка

стояк: К1 — канализация, В1 — ХВС, Т3 — ГВС

1 — номер помещения, площадь м²

Итого розеток (механизмов) — 56 шт; рамок — 44 шт: на 1 пост — 32, на 2 поста — 12.

Допущения и предложения на листе. Основа листа: планировка по обводу плана заказчика, не замерена (К-1); высота до плиты 2650 мм от чистого пола — решение автора (ИЗ-1); отметки плана потолков сдвинуты на -95 мм (+2.745 плана = низ плиты), не замерено (К-2); толщины стен приняты: наружные 260 мм, перегородки 130 мм (К-1); положение стен и проёмов — по брифу без обмера и плана БТИ (К-1); разрешённая мощность 10 кВт принята, ТУ не переданы (К-6); вентканалы приняты, в брифе не заданы (К-5); тип дома, перекрытие и несущие стены не известны — документов нет (К-3); плита электрическая — принята, в брифе не указано (К-6); система заземления TN-C-S принята, ТУ не переданы (К-6); число жильцов 2 принято, в брифе не указано (К-9); подрайон климата не задан — принят не северный (жилые от 2,5 м) (К-26). Знак «*» — принято, не замерено (замерить): К-4: Ст К1-1, Ст В1-2, Ст Т3-3. Знак «**» — предложено, не утверждено (согласовать): ЭВ10, TP1, ЭВ9, TP2, P7, ЭВ11, ЭВ12, ЭВ4, ЭВ13, ЭВ5, ЭВ14, КУП1, КУП2. См. лист открытых вопросов (лист 5, записи К-1, К-3–К-6, К-8, К-9; лист 6, запись К-26).

Примечания

1. За отметку 0,000 принят уровень чистого пола. Высоты H — от чистого пола до оси изделия; привязки — от чистовой грани стены до оси механизма (у рамки на несколько постов — до оси рамки).
2. Розетки без отметки H у знака — на высоте 300 мм от чистого пола до оси механизма; выводы кабеля — по паспорту прибора.
3. Розетки в санузле — только вне зон 0–2 (ПУЭ 7.1.48, ГОСТ Р 50571.7.701-2024), IP44, через УЗО 30 мА.
4. Розеточные и мокрые линии — через УЗО или дифавтомат с током утечки не более 30 мА (ПУЭ 7.1.79); в санузле выполнить ДСУП (ПУЭ 7.1.87–7.1.88).
5. Кабель — медный, исполнение нг(A)-LS (ГОСТ 31565-2012); скрытая прокладка только горизонтально и вертикально, фактические трассы зафиксировать исполнительной схемой до закрытия отделкой.
6. Расчёт нагрузок, токов КЗ, селективности и сечений — по проекту ЭОМ организации с допуском СРО; лист задаёт состав, расположение и группы.
7. Выводы кухонной техники — после утверждения проекта кухни (ориентировочно); привязки выводов даны от осей модулей гарнитура и пересматриваются вместе с проектом кухни.
8. Ведомости электроточек, изделий, светильников и расшифровка клавиш — лист 26.

1000 мм · печать 1:1

Изм.	Кол.уч	Лист	№ док.	Подп.	Дата
Разраб.		Кырлан А.С.			04.11.26
Пров.					
ГИП					
Н. контр.					
Утв.					

ГД-2026-020-АИ

Квартира 68 м², элитный модерн

Общая площадь 68,47* м² · * размеры приняты, не замерены (реестр — л. 5–7, К-1)

Дизайн-проект интерьера

Стадия	Лист	Листов
РП	23	105

План розеток и электровыводов

М 1:50


Кырлан Александр Сергеевич

выпуск 04.11.2026 № 8be4ef4c81 · стр. 26 из 117

План освещения

Светильники, группы включения, извещатели · размеры в мм

ПРЕДВАРИТЕЛЬНО · не для производства работ · открыто пунктов: 25 (реестр — л. 5–7)

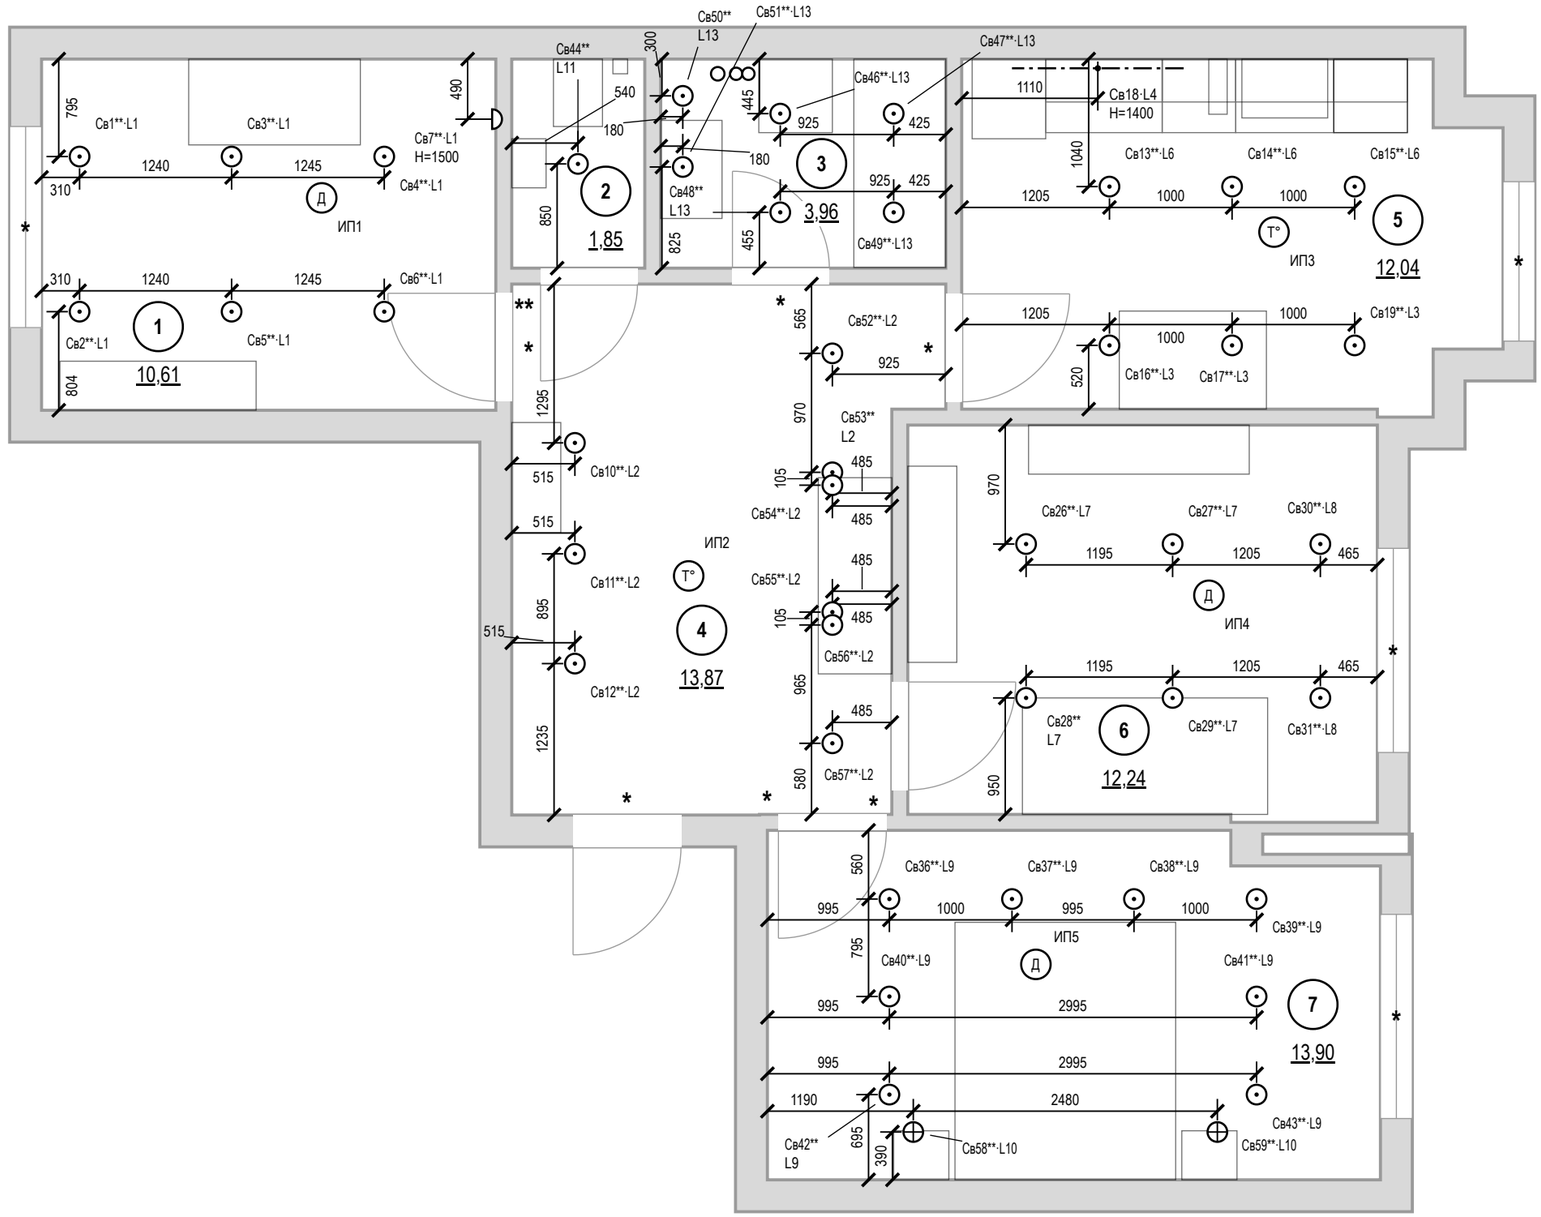

Условные обозначения

- светильник встраиваемый точечный
- светильник подвесной
- светильник настенный (бра), H — высота оси
- линейный светильник настенный (подсветка столешницы), точка — вывод питания
- Св1·L1 — марка светильника (как в ведомости и на развёртках) · группа включения L (лист 25)
- Д — извещатель пожарный дымовой автономный
- Т° — извещатель пожарный тепловой
- мебель и сантехприборы — подложка
- стояк: К1 — канализация, В1 — ХВС, Т3 — ГВС
- 1 — номер помещения, площадь м²

Допущения и предложения на листе

Основа листа: планировка по обводу плана заказчика, не замерена (К-1); высота до плиты 2650 мм от чистого пола — решение автора (ИЗ-1); отметки плана потолков сдвинуты на -95 мм (+2.745 плана = низ плиты), не замерено (К-2); толщины стен приняты: наружные 260 мм, перегородки 130 мм (К-1); положение стен и проёмов — по брифу без обмера и плана БТИ (К-1); разрешённая мощность 10 кВт принята, ТУ не переданы (К-6); вентканалы приняты, в брифе не заданы (К-5); тип дома, перекрытие и несущие стены не известны — документов нет (К-3); плита электрическая — принята, в брифе не указано (К-6); система заземления TN-C-S принята, ТУ не переданы (К-6); число жильцов 2 принято, в брифе не указано (К-9); подрайон климата не задан — принят не северный (жилые от 2,5 м) (К-26).

Знак «*» — принято, не замерено и не подтверждено (замерить на объекте): К-1: окно пом. 1 (стена Г), 5 (Б), 6 (Б), 7 (Б) — окно: положение, ширина, высота и подоконник приняты по обводу плана заказчика, без обмера, не замерены; дверь пом. 1 (стена Б), 3 (В), 5 (Г), 6 (Г), 7 (А) — проём принят по обводу плана заказчика, без обмера: положение и ширина сняты с плана, не замерены; дверь пом. 4 (стена В) — входная дверь: положение и ширина проёма приняты по обводу плана заказчика, без обмера, не замерены; К-4: Ст К1-1, Ст В1-2, Ст Т3-3 — положение стояка снято с обвода плана, не замерено.

Знак «**» — предложение проектировщика, заказчиком не утверждено (согласовать с заказчиком): К-1: дверь пом. 2 (стена В) — проём принят по обводу плана заказчика, без обмера: положение и ширина сняты с плана, не замерены; открывание наружу (в прихожую): санузел 1,1 м — внутрь полотно задевает раковину П14; К-20: Св1, Св2, Св3, Св4, Св5, Св6, Св7, Св44, Св46, Св47, Св48, Св49, Св50, Св51, Св10, Св11, Св12, Св13, Св14, Св15, Св16, Св17, Св19, Св26, Св27, Св28, Св29, Св30, Св31, Св36, Св37, Св38, Св39, Св40, Св41, Св42, Св43, Св58, Св59 — место и марка — по исходному плану потолков (±30 мм по рисунку); тип, мощность и цвет света — допущение исполнителя; Св52, Св53, Св54, Св55, Св56, Св57 — место и марка — по исходному плану потолков (±30 мм по рисунку); тип, мощность и цвет света — допущение исполнителя; в нише по плите (ж/б) встроить некуда — накладные.

Открытые вопросы и конфликты по листу: К-20.

См. лист открытых вопросов (лист 5, записи К-1, К-3–К-6, К-9; лист 6, записи К-20, К-26).

Примечания

1. За отметку 0,000 принят уровень чистого пола. Высоты H — от чистого пола до оси изделия; привязки — от чистовой грани стены до оси механизма (у рамки на несколько постов — до оси рамки).
2. Высота установки, не указанная на плане: светильники — на потолке; настенные — по отметке H у знака. Привязки — до оси светильника от чистовой грани стены, по рядам.
3. Во влажных помещениях — светильники не ниже IP44; в зонах 0–2 ванной — по ГОСТ Р 50571.7.701-2024 (зона 1 — IPX5).
4. Розеточные и мокрые линии — через УЗО или дифавтомат с током утечки не более 30 мА (ПУЭ 7.1.79); в санузле выполнить ДСУП (ПУЭ 7.1.87–7.1.88).
5. Кабель — медный, исполнение нг(А)-LS (ГОСТ 31565-2012); скрытая прокладка только горизонтально и вертикально, фактические трассы зафиксировать исполнительной схемой до закрытия отделкой.
6. Расчёт нагрузок, токов КЗ, селективности и сечений — по проекту ЭОМ организации с допуском СРО; лист задаёт состав, расположение и группы.
7. Ведомость светильников (тип, количество, мощность, поток, Tц, Ra) — лист 44.
8. Оценка освещённости (по норме СанПиН 1.2.3685-21, табл. 5.52, на полу; не светотехнический расчёт, декоративная подсветка в оценку не входит) — лист 26.

1000 мм · печать 1:1

Изм.	Кол.уч	Лист	№ док.	Подп.	Дата
Разраб.		Кырлан А.С.			04.11.26
Пров.					
ГИП					
Н. контр.					
Утв.					

ГД-2026-020-АИ

Квартира 68 м², элитный модерн

Общая площадь 68,47* м² · * размеры приняты, не замерены (реестр — л. 5–7, К-1)

Дизайн-проект интерьера

Стадия	Лист	Листов
РП	24	105

План освещения

М 1:50


Кырлан Александр Сергеевич

выпуск 04.11.2026 № 8be4ef4c81 · стр. 27 из 117

План выключателей и схема включения

Выключатели S, группы включения L, линии связи · размеры в мм

ПРЕДВАРИТЕЛЬНО · не для производства работ · открыто пунктов: 25 (реестр — л. 5–7)

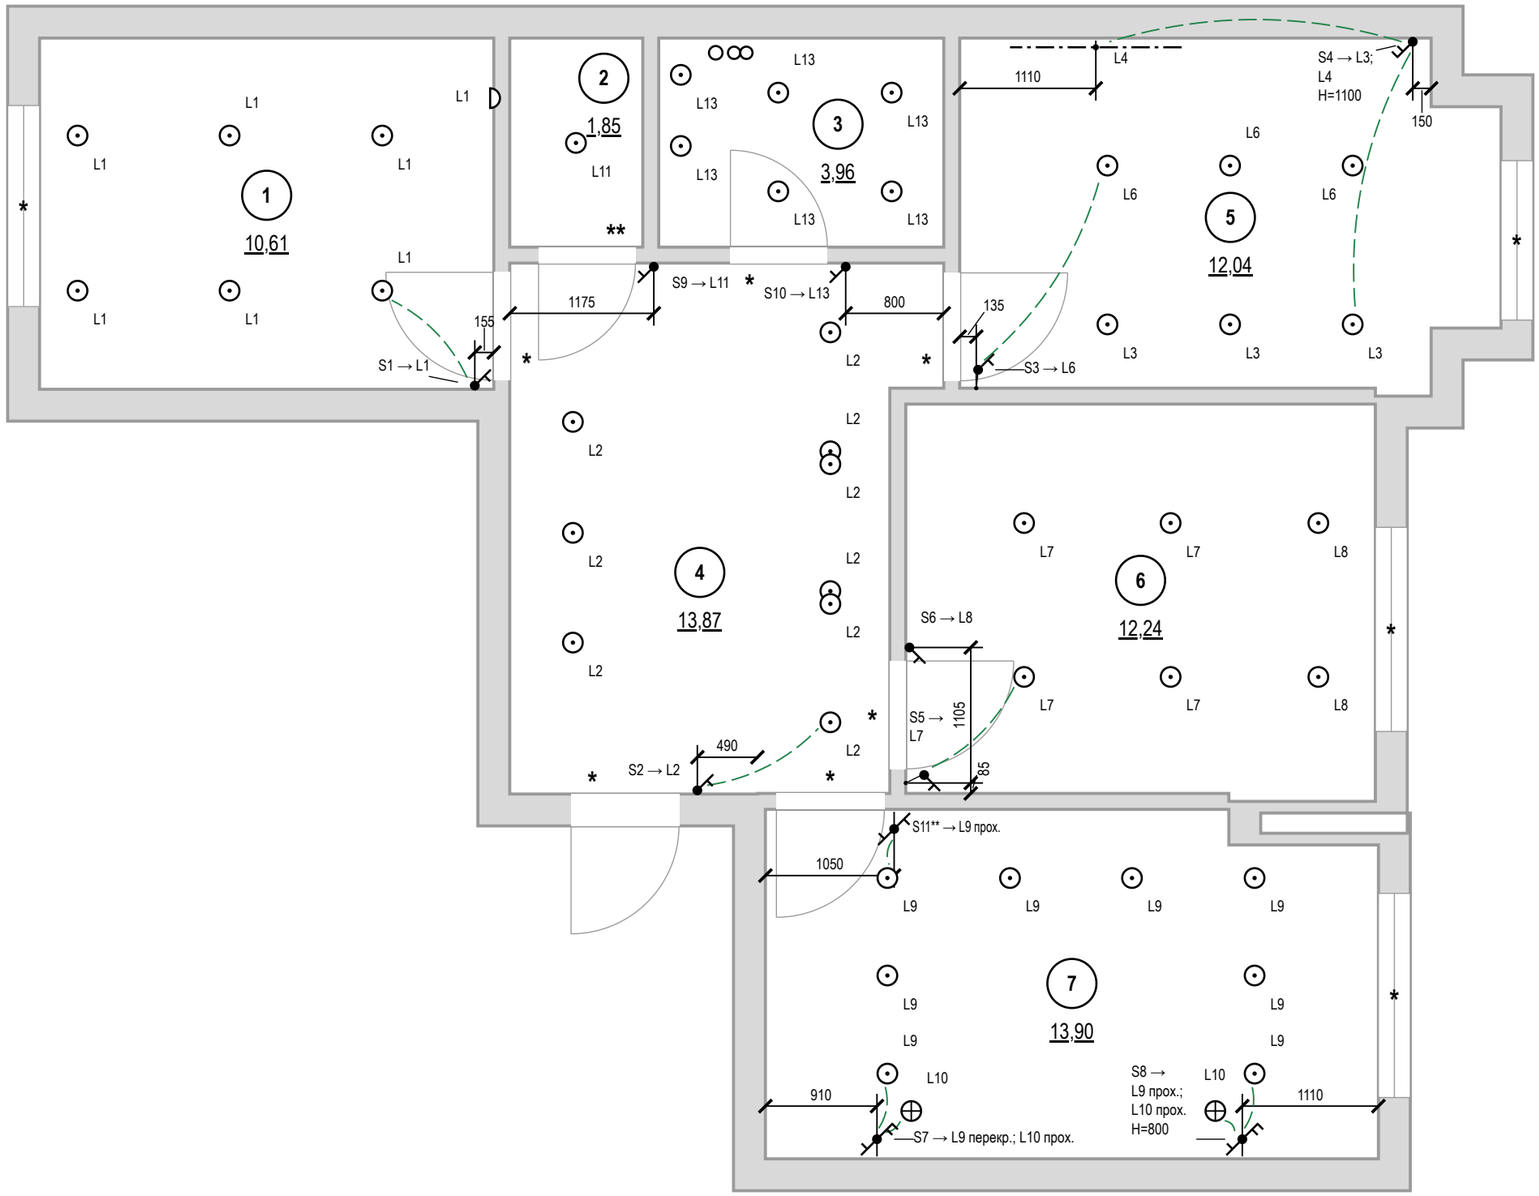

Условные обозначения

- выключатель одноклавишный
- выключатель двухклавишный (флажков — по числу клавиш)
- выключатель с проходной или перекрёстной клавишей (обратный флажок); тип клавиши — в подписи
- S1 → — марка → группы по клавишам (через «;»): прох. — проходной, перекр. — перекрёстный, дим. — светорегулятор; Н — высота
- связь: выключатель → ближайший светильник группы в том же помещении (не трасса кабеля); полный состав группы — по номеру L
- светильник встраиваемый точечный
- светильник подвесной
- светильник настенный (бра), Н — высота оси
- линейный светильник настенный (подсветка столешницы), точка — вывод питания
- L1 — группа включения у светильника
- стояк: К1 — канализация, В1 — ХВС, Т3 — ГВС
- 1 — номер помещения, площадь м²

Допущения и предложения на листе

Основа листа: планировка по обводу плана заказчика, не замерена (К-1); высота до плиты 2650 мм от чистого пола — решение автора (ИЗ-1); отметки плана потолков сдвинуты на -95 мм (+2.745 плана = низ плиты), не замерено (К-2); толщины стен приняты: наружные 260 мм, перегородки 130 мм (К-1); положение стен и проёмов — по брифу без обмера и плана БТИ (К-1); разрешённая мощность 10 кВт принята, ТУ не переданы (К-6); вентканалы приняты, в брифе не заданы (К-5); тип дома, перекрытие и несущие стены не известны — документов нет (К-3); плита электрическая — принята, в брифе не указано (К-6); система заземления TN-C-S принята, ТУ не переданы (К-6); число жильцов 2 принято, в брифе не указано (К-9); подрайон климата не задан — принят не северный (жилые от 2,5 м) (К-26).

Знак «*» — принято, не замерено и не подтверждено (замерить на объекте): К-1: окно пом. 1 (стена Г), 5 (Б), 6 (Б), 7 (Б) — окно: положение, ширина, высота и подоконник приняты по обводу плана заказчика, без обмера, не замерены; дверь пом. 1 (стена Б), 3 (В), 5 (Г), 6 (Г), 7 (А) — проём принят по обводу плана заказчика, без обмера: положение и ширина сняты с плана, не замерены; дверь пом. 4 (стена В) — входная дверь: положение и ширина проёма приняты по обводу плана заказчика, без обмера, не замерены; К-4: Ст К1-1, Ст В1-2, Ст Т3-3 — положение стояка снято с обвода плана, не замерено.

Знак «**» — предложение проектировщика, заказчиком не утверждено (согласовать с заказчиком): S11 — у входа в спальню нужен выключатель основного света 08-А/08-Б, прикроватные — проходные; К-1: дверь пом. 2 (стена В) — проём принят по обводу плана заказчика, без обмера: положение и ширина сняты с плана, не замерены; открывание наружу (в прихожую): санузел 1,1 м — внутрь полотно задевает раковину П14.

См. лист открытых вопросов (лист 5, записи К-1, К-3–К-6, К-9; лист 6, запись К-26).

Примечания

1. За отметку 0,000 принят уровень чистого пола. Высоты Н — от чистого пола до оси изделия; привязки — от чистовой грани стены до оси механизма (у рамки на несколько постов — до оси рамки).
2. Высота установки, не указанная на плане: выключатели — 900 мм от чистого пола (у кровати и другие — Н у марки), со стороны дверной ручки (ПУЭ 7.1.51).
3. Какой выключатель какие светильники включает — по номеру группы L: у выключателя (S1 → L1; L2 — клавиши по порядку) и у каждого светильника. Пунктир подсказка к ближайшему светильнику группы в том же помещении (не дальше 3 м), это не трасса кабеля; выключатель за стеной (у двери санузла) и далёкая группа — только номер группы.
4. Группы из нескольких мест (L9 — S7, S8, S11**; L10 — S7, S8): на крайних местах — проходные клавиши, на промежуточных — перекрёстные; механизмы — в ведомости изделий.
5. Розеточные и мокрые линии — через УЗО или дифавтомат с током утечки не более 30 мА (ПУЭ 7.1.79); в санузле выполнить ДСУП (ПУЭ 7.1.87–7.1.88).
6. Кабель — медный, исполнение нг(А)-LS (ГОСТ 31565-2012); скрытая прокладка только горизонтально и вертикально, фактические трассы зафиксировать исполнительной схемой до закрытия отделкой.
7. Расчёт нагрузок, токов КЗ, селективности и сечений — по проекту ЭОМ организации с допуском СРО; лист задаёт состав, расположение и группы.
8. Расшифровка клавиш и ведомость изделий — лист 26.

1000 мм · печать 1:1

Изм.	Кол.уч	Лист	№ док.	Подп.	Дата
Разраб.		Кырлан А.С.			04.11.26
Пров.					
ГИП					
Н. контр.					
Утв.					

ГД-2026-020-АИ

Квартира 68 м², элитный модерн

Общая площадь 68,47* м² · * размеры приняты, не замерены (реестр — л. 5–7, К-1)

Дизайн-проект интерьера

Стадия	Лист	Листов
РП	25	105

План выключателей и схема включения

М 1:50

Кырлан Александр Сергеевич

выпуск 04.11.2026 № 8be4ef4c81 · стр. 28 из 117

Ведомость электроточек и изделий

Электроточки, изделия, светильники, освещённость, клавиши выключателей · б/м

Ведомость электроточек

Марка	Пом.	Назначение	Н, мм	Гр.
Р1	1	рабочий стол	900	3
Р2	1	рабочий стол: монитор	900	3
Р3	1	уборка	300	3
Р23	1	рабочий стол: компьютер, монитор, зарядки	900	3
Р24	1	рабочий стол: компьютер, монитор, зарядки	900	3
Р25	1	уборка у входа	300	3
Р26	1	общего назначения	300	3
Р27	1	общего назначения	300	3
ЭВ10**	1	электрокарниз (привод штор)	2450	3
КУП1**	2	КУП — уравнивание потенциалов (ДСУП)	300	
Р19	2	розетка у раковины (фен, зона 3), IP44	1100	15
ЭВ6	2	вентилятор в потолке (знак 11 по исходному плану; вывод — в запотолочное пространство) ВР1 (клавиша L11, таймер выбега)	2400	2
КУП2**	3	КУП — уравнивание потенциалов (ДСУП)	300	
Р20	3	фен у умывальника, IP44	1100	15
Р45	3	стиральная машина, IP44	1100	20
ТР1**	3	терморегулятор тёплого пола, IP44	1000	19
ЭВ8	3	вентилятор в потолке (знак 11 по исходному плану; вывод — в запотолочное пространство) ВР2 (клавиша L13, таймер выбега)	2400	2
Р4	4	питание слаботочного щита (роутер, ONT)	1300	16
Р5	4	уборка, сушилка обуви	300	7
Р29	4	уборка у входа	300	16
Р30	4	прихожая: зарядка телефона и ключей	900	16
Р31	4	у обувной полки (сушка обуви)	300	16
Р32	4	док-станция робота-пылесоса	300	16
ТР2**	4	терморегулятор тёплого пола	1000	19
ЩК	4	щит квартирный ЩРВ-П-72, IP41	1700	

Ведомость электроточек (продолжение)

Марка	Пом.	Назначение	Н, мм	Гр.
ЭВ9**	4	контроллер защиты от протечек и питание электрокранов (у слаботочного щита)	1300	16
Р6	5	посудомоечная машина (в нише М12, сбоку от корпуса, доступ через цоколь)	300	14
Р7**	5	холодильник — над нишей, съёмная панель	2050	10
Р8	5	чайник и кофемашина (отдельная линия)	1100	9
Р9	5	фартук: мелкая техника	1100	8
Р10	5	общего назначения	300	4
Р21	5	фартук	1100	8
Р22	5	фартук	1100	8
Р33	5	уборка у входа	300	8
ЭВ1	5	варочная панель — в соседнем модуле, за ящиком	600	12
ЭВ2	5	духовой шкаф — в цоколе	150	13
ЭВ3	5	вытяжка — над корпусом	2200	11
ЭВ11**	5	измельчитель мойки	300	8
ЭВ12**	5	подсветка навесных шкафов (блок питания ленты)	2450	8
Р11	6	ТВ, приставка	1100	5
Р12	6	саундбар	1100	5
Р13	6	торшер у дивана	300	5
Р14	6	у дивана: зарядка	300	5
Р15	6	уборка	300	5
Р34	6	ТВ-зона: приставка, консоль, саундбар	1000	5
Р35	6	ТВ-зона: приставка, консоль, саундбар	1000	5
Р36	6	у дивана: торшер, зарядка	300	5
Р37	6	у дивана: торшер, зарядка	300	5
ЭВ4**	6	кондиционер КВ-1** — вывод питания внутреннего блока	2295	17
ЭВ13**	6	электрокарниз (привод штор)	2450	5
Р16	7	у кровати: лампа, зарядка	600	6

Ведомость электроточек (продолжение)

Марка	Пом.	Назначение	Н, мм	Гр.
Р17	7	у кровати: лампа, зарядка	600	6
Р18	7	уборка	300	6
Р38	7	общего назначения	300	6
Р39	7	общего назначения	300	6
Р40	7	общего назначения	300	6
Р41	7	общего назначения	300	6
Р42	7	общего назначения	300	6
Р43	7	общего назначения	300	6
Р44	7	общего назначения	300	6
ЭВ5**	7	кондиционер КВ-2** — вывод питания внутреннего блока	2295	18
ЭВ14**	7	электрокарниз (привод штор)	2450	6

Ведомость изделий

Наименование	Марки	Ед.	Кол.
Розетка с з/к и защитными шторками, 16 А	по ведомости точек	шт	53
Розетка IP44 с крышкой, 16 А	Р19, Р20, Р45	шт	3
Выключатель 1-клав.	S1–S3, S5, S6, S9, S10	шт	7
Выключатель 1-клав. проходной	S11**	шт	1
Выключатель 2-клав.	S4	шт	1
Выключатель 2-клав. (перекрёстная + проходная)	S7	шт	1
Выключатель 2-клав. проходной	S8	шт	1
Рамка 1-постовая	в т. ч. 11 под выключ.	шт	43
Рамка 2-постовая		шт	12
Терморегулятор тёплого пола	ТР1**, ТР2**	шт	2
Коробка установочная (подрозетник) Ø68	розетки, выключатели	шт	69
Вывод кабеля под прибор (клеммник)	ЭВ1–ЭВ3, ЭВ4**, ЭВ5**, ЭВ6, ЭВ8, ЭВ9**, ЭВ10**, ЭВ11**, ЭВ12**, ЭВ13**, ЭВ14**	шт	13
Коробка уравнивания потенциалов КУП	КУП1**, КУП2**	шт	2
Извещатель дымовой автономный	ИП1, ИП4, ИП5	шт	3

Ведомость изделий (продолжение)

Наименование	Марки	Ед.	Кол.
Извещатель тепловой	ИП2, ИП3	шт	2
Щит квартирный (состав — лист щита)	ЩК	шт	1
Розетка компьютерная RJ45, кат. 6, с рамкой и подрозетником	LAN1, LAN2	шт	2
Розетка телевизионная (коаксиальная) с рамкой и подрозетником	ТВ1	шт	1
Точка доступа Wi-Fi (оборудование заказчика), питание PoE	АР1**	шт	1
Трубка или монитор домофона (поставка домофонной организации)	ДФ1	шт	1
Щит слаботочный ЩС**: корпус, DIN-рейка, розетки 220 В	ЩС**	шт	1
Патч-панель, портов не менее 3		шт	1
Коммутатор, портов не менее 3, из них PoE 1		шт	1
Кабель домофона — тип по системе поставщика (по лучам от ЩС**, запас 10 %)		м	3,1
Кабель коаксиальный RG-6 (75 Ом) к розеткам ТВ (по лучам от ЩС**, запас 10 %)		м	14,1
Кабель U/UTP кат. 5e (LAN, Wi-Fi и камеры по PoE) (по лучам от ЩС**, запас 10 %)		м	27,4
Кабель U/UTP кат. 6 (LAN, Wi-Fi и камеры по PoE) (по лучам от ЩС**, запас 10 %)		м	2,7

Допущения и предложения на листе. Основа листа: планировка по обводу плана заказчика, не замерена (К-1); высота до плиты 2650 мм от чистого пола — решение автора (ИЗ-1); отметки плана потолков сдвинуты на -95 мм (+2.745 плана = низ плиты), не замерено (К-2); толщины стен приняты: наружные 260 мм, перегородки 130 мм (К-1); положение стен и проёмов — по брифу без обмера и плана БТИ (К-1); разрешённая мощность 10 кВт принята, ТУ не переданы (К-6); вентканалы приняты, в брифе не заданы (К-5); тип дома, перекрытие и несущие стены не известны — документов нет (К-3); плита электрическая — принята, в брифе не указано (К-6); система заземления TN-C-S принята, ТУ не переданы (К-6); число жильцов 2 принято, в брифе не указано (К-9); подрайон климата не задан — принят не северный (жилые от 2,5 м) (К-26). Знак «**» — предложено, не утверждено (согласовать): ЭВ10, ТР1, ЭВ9, ТР2, Р7, ЭВ11, ЭВ12, КВ-1, ЭВ4, ЭВ13, КВ-2, ЭВ5, ЭВ14, S11, КУП1, КУП2, ЩС, АР1. См. лист открытых вопросов (лист 5, записи К-1, К-3, К-5, К-6, К-9; лист 6, запись К-26).

Примечания

1. Ведомости сведены с планов розеток, освещения и выключателей; марки, группы и высоты — те же, что у знаков на планах.
2. Механизмы, рамки и светорегуляторы — одной серии; число постов и клавиш сверено с выбранной серией. Перекрёстная клавиша — отдельный механизм серии.
3. Освещённость (оценка) — по норме СанПиН 1.2.3685-21 (табл. 5.52, на полу), не светотехнический расчёт; декоративная подсветка в оценку не входит.
4. За отметку 0,000 принят уровень чистого пола. Высоты Н — от чистого пола до оси изделия; привязки — от чистовой грани стены до оси механизма (у рамки на несколько постов — до оси рамки).
5. Розеточные и мокрые линии — через УЗО или дифавтомат с током утечки не более 30 мА (ПУЭ 7.1.79); в санузле выполнить ДСУП (ПУЭ 7.1.87–7.1.88).
6. Кабель — медный, исполнение нг(А)-LS (ГОСТ 31565-2012); скрытая прокладка только горизонтально и вертикально, фактические трассы зафиксировать исполнительной схемой до закрытия отделкой.
7. Расчёт нагрузок, токов КЗ, селективности и сечений — по проекту ЭОМ организации с допуском СРО; лист задаёт состав, расположение и группы.
8. Ведомости занимают 2 листов этого наименования: таблицы, не вошедшие в поле листа, продолжены на следующем листе.

Изм.	Кол.уч	Лист	№ док.	Подп.	Дата
Разраб.		Кырлан А.С.			04.11.26
Пров.					
ГИП					
Н. контр.					
Утв.					

ГД-2026-020-АИ

Квартира 68 м², элитный модерн

Общая площадь 68,47* м² · * размеры приняты, не замерены (реестр — л. 5–7, К-1)

Дизайн-проект интерьера

Стадия	Лист	Листов
РП	26	105

Ведомость электроточек и изделий

М б/м

Кырлан Александр Сергеевич

выпуск 04.11.2026 № 8be4ef4c81 · стр. 29 из 117

Ведомость электроточек и изделий (продолжение)

Электроточки, изделия, светильники, освещённость, клавиши выключателей · б/м

Ведомость светильников

Поз.	Марки	Тип	Кол.	P, Вт	Ф, лм	IP	Тц/Ra
1	Св1**, Св2**, Св3**, Св4**, Св5**, Св6**, Св10**, Св11**, Св12**, Св13**, Св14**, Св15**, Св16**, Св17**, Св19**, Св26**, Св27**, Св28**, Св29**, Св30**, Св31**, Св36**, Св37**, Св38**, Св39**, Св40**, Св41**, Св42**, Св43**	встраиваемый точечный	29	7	600		2700/90
2	Св7**	настенный (бра), H=1500	1	5	300		2700/90
3	Св44**, Св46**, Св47**, Св48**, Св49**, Св50**, Св51**	встраиваемый точечный	7	7	600	44	2700/90
4	Св52**, Св53**, Св54**, Св55**, Св56**, Св57**	встраиваемый точечный	6	5	400		2700/90
5	Св18	линейный светильник, H=1400	1	30	2400		2700/90
6	Св58**, Св59**	подвесной	2	6	400		2700/90

Освещённость (оценка)

Пом.	S, м²	Ен, лк	Ф треб., лм	Ф по пр., лм
1	10,6	300	8970	3600
2	1,9	50	260	600
3	4	50	560	3600
4	13,9	50	1950	4200
5	12	150	5090	3600
6	12,2	150	5170	3600
7	13,9	150	5870	5600

Расшифровка клавиш

Марка	Пом.	H, мм	Клав.	Механизм	Группа: светильники
S1	1	900	1	обычный	L1: Св1**, Св2**, Св3**, Св4**, Св5**, Св6**, Св7**
S2	4	900	1	обычный	L2: Св10**, Св11**, Св12**, Св52**, Св53**, Св54**, Св55**, Св56**, Св57**
S3	5	900	1	обычный	L6: Св13**, Св14**, Св15**
S4	5	1100	1	обычный	L3: Св16**, Св17**, Св19**
			2	обычный	L4: Св18
S5	6	900	1	обычный	L7: Св26**, Св27**, Св28**, Св29**
S6	6	900	1	обычный	L8: Св30**, Св31**
S7	7	900	1	перекрёстный	L9: Св36**, Св37**, Св38**, Св39**, Св40**, Св41**, Св42**, Св43**
			2	проходной	L10: Св58**, Св59**
S8	7	800	1	проходной	L9: Св36**, Св37**, Св38**, Св39**, Св40**, Св41**, Св42**, Св43**
			2	проходной	L10: Св58**, Св59**
S9	4	900	1	обычный	L11: Св44**
S10	4	900	1	обычный	L13: Св46**, Св47**, Св48**, Св49**, Св50**, Св51**
S11**	7	900	1	проходной	L9: Св36**, Св37**, Св38**, Св39**, Св40**, Св41**, Св42**, Св43**

Допущения и предложения на листе

Основа листа: планировка по обводу плана заказчика, не замерена (К-1); высота до плиты 2650 мм от чистого пола — решение автора (ИЗ-1); отметки плана потолков сдвинуты на -95 мм (+2.745 плана = низ плиты), не замерено (К-2); толщины стен приняты: наружные 260 мм, перегородки 130 мм (К-1); положение стен и проёмов — по брифу без обмера и плана БТИ (К-1); разрешённая мощность 10 кВт принята, ТУ не переданы (К-6); вентканалы приняты, в брифе не заданы (К-5); тип дома, перекрытие и несущие стены не известны — документов нет (К-3); плита электрическая — принята, в брифе не указано (К-6); система заземления TN-C-S принята, ТУ не переданы (К-6); число жильцов 2 принято, в брифе не указано (К-9); подрайон климата не задан — принят не северный (жилые от 2,5 м) (К-26).

Знак «**» — предложение проектировщика, заказчиком не утверждено (согласовать с заказчиком): S11 — у входа в спальню нужен выключатель основного света 08-А/08-Б, прикроватные — проходные; К-20: Св1, Св2, Св3, Св4, Св5, Св6, Св7, Св44, Св46, Св47, Св48, Св49, Св50, Св51, Св10, Св11, Св12, Св13, Св14, Св15, Св16, Св17, Св19, Св26, Св27, Св28, Св29, Св30, Св31, Св36, Св37, Св38, Св39, Св40, Св41, Св42, Св43, Св58, Св59 — место и марка — по исходному плану потолков (±30 мм по рисунку); тип, мощность и цвет света — допущение исполнителя; Св52, Св53, Св54, Св55, Св56, Св57 — место и марка — по исходному плану потолков (±30 мм по рисунку); тип, мощность и цвет света — допущение исполнителя; в нише по плите (ж/б) встроить некуда — накладные.

См. лист открытых вопросов (лист 5, записи К-1, К-3, К-5, К-6, К-9; лист 6, записи К-20, К-26).

Примечания

1. Продолжение ведомостей: лист 2 из 2 этого наименования; таблицы, прерванные на предыдущем листе, продолжены с заголовком «(продолжение)».
2. За отметку 0,000 принят уровень чистого пола. Высоты H — от чистого пола до оси изделия; привязки — от чистовой грани стены до оси механизма (у рамки на несколько постов — до оси рамки).
3. Розеточные и мокрые линии — через УЗО или дифавтомат с током утечки не более 30 мА (ПУЭ 7.1.79); в санузле выполнить ДСУП (ПУЭ 7.1.87–7.1.88).
4. Кабель — медный, исполнение нг(А)-LS (ГОСТ 31565-2012); скрытая прокладка только горизонтально и вертикально, фактические трассы зафиксировать исполнительной схемой до закрытия отделкой.
5. Расчёт нагрузок, токов КЗ, селективности и сечений — по проекту ЭОМ организации с допуском СРО; лист задаёт состав, расположение и группы.

Изм.	Кол.уч	Лист	№ док.	Подп.	Дата
Разраб.		Кырлан А.С.			04.11.26
Пров.					
ГИП					
Н. контр.					
Утв.					

ГД-2026-020-АИ

Квартира 68 м², элитный модерн

Общая площадь 68,47* м² · * размеры приняты, не замерены (реестр — л. 5–7, К-1)

Дизайн-проект интерьера

Стадия	Лист	Листов
РП	27	105

Ведомость электроточек и изделий (продолжение)


М б/м

Кырлан Александр Сергеевич

выпуск 04.11.2026 № 8be4ef4c81 · стр. 30 из 117

Однолинейная схема щита

Щит квартирный ЩК · гр. 1—10 из 20 · без масштаба

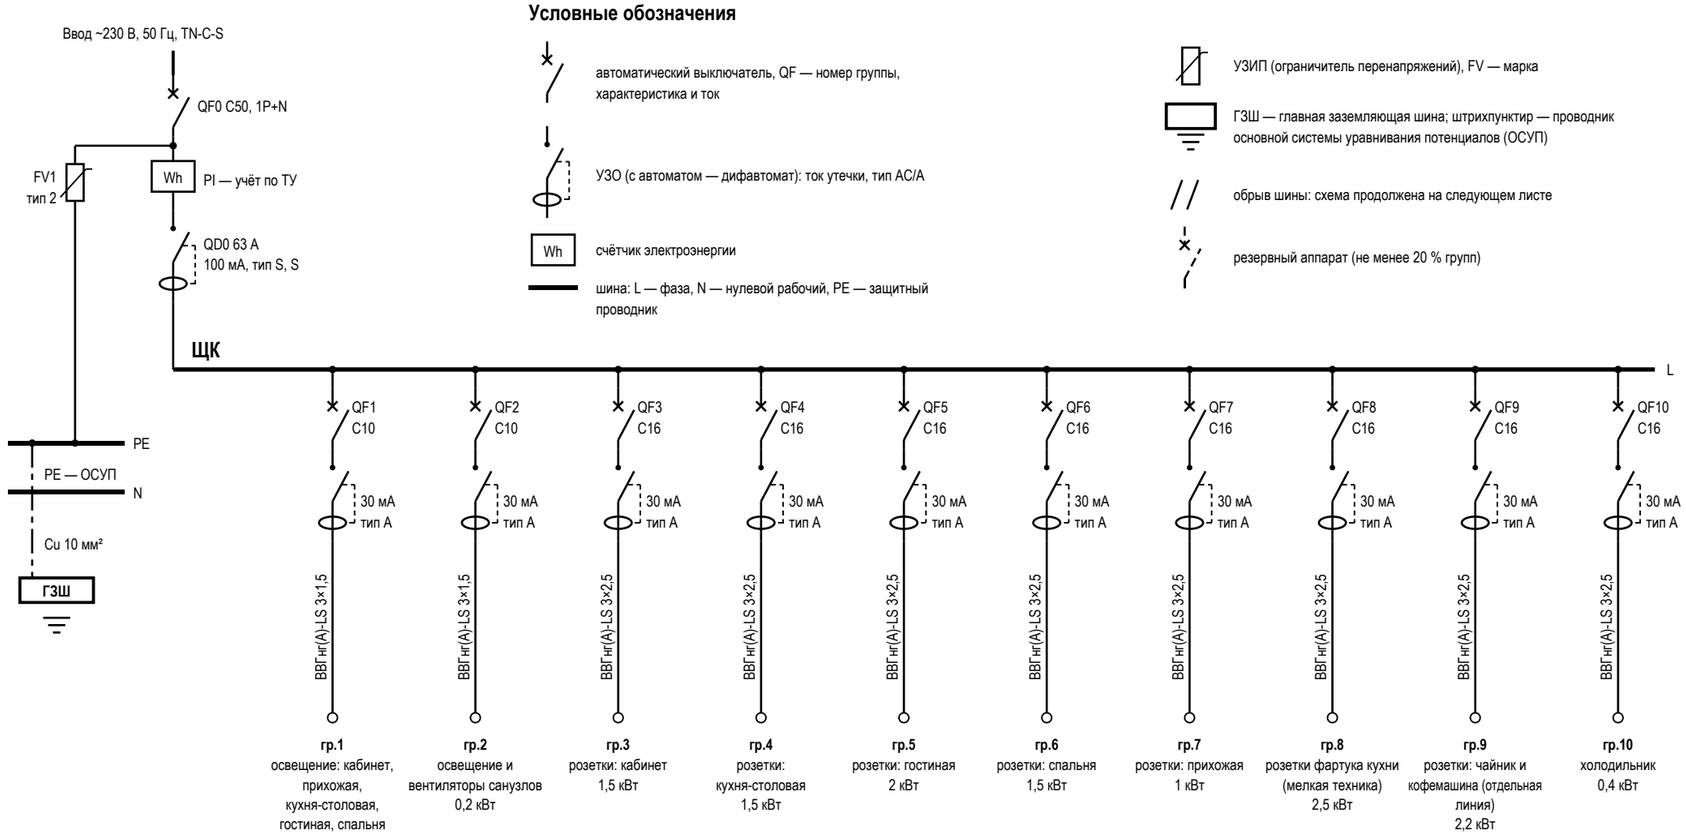

Условные обозначения

- автоматический выключатель, QF — номер группы, характеристика и ток
- УЗО (с автоматом — дифавтомат): ток утечки, тип AC/A
- Wh — счётчик электроэнергии
- шина: L — фаза, N — нулевой рабочий, PE — защитный проводник
- УЗИП (ограничитель перенапряжений), FV — марка
- ГЗШ — главная заземляющая шина; штрихпунктир — проводник основной системы уравнивания потенциалов (ОСУП)
- обрыв шины: схема продолжена на следующем листе
- резервный аппарат (не менее 20 % групп)

Данные щитка

Показатель	Значение
Номер щитка	ЩК
Тип	ЩРВ-П-72, IP41
Уст. мощность, кВт	33,1
Разреш. мощность, кВт	10
Расчётная, кВт	10,8
Расчётная > разрешённой	10,8 > 10 кВт: превышение 0,8 кВт
Автоматы 1п: занят. / рез.	20 / 4
Модулей: всего / занято	72 / 46
Ток на вводе, А	50
Вводной аппарат	QF0 C50, 1P+N
УЗИП	FV1, тип 2, ЩК, после счётчика
ГЗШ, проводник ОСУП	Cu 10 мм²
Листов схемы	2 (группы по листам)

Таблица групп щита ЩК и кабельный журнал

№	Назначение	Помещения	Автомат	УЗО / дифавтомат	Кабель	Длина, м	P, кВт	Точек
1	освещение: кабинет, прихожая, кухня-столовая, гостиная, спальня	1, 4, 5, 6, 7	C10	30 мА, тип A	ВВГнг(A)-LS 3×1,5	85	0,6	48
2	освещение и вентиляторы санузлов	2, 3, 4	C10	30 мА, тип A	ВВГнг(A)-LS 3×1,5	36	0,2	11
3	розетки: кабинет	1	C16	30 мА, тип A	ВВГнг(A)-LS 3×2,5	41	1,5	9
4	розетки: кухня-столовая	5	C16	30 мА, тип A	ВВГнг(A)-LS 3×2,5	41	1,5	1
5	розетки: гостиная	6	C16	30 мА, тип A	ВВГнг(A)-LS 3×2,5	41	2	10
6	розетки: спальня	7	C16	30 мА, тип A	ВВГнг(A)-LS 3×2,5	41	1,5	11
7	розетки: прихожая	4	C16	30 мА, тип A	ВВГнг(A)-LS 3×2,5	30	1	1
8	розетки фартука кухни (мелкая техника)	5	C16	30 мА, тип A	ВВГнг(A)-LS 3×2,5	18	2,5	6
9	розетки: чайник и кофемашина (отдельная линия)	5	C16	30 мА, тип A	ВВГнг(A)-LS 3×2,5	18	2,2	1
10	холодильник	5	C16	30 мА, тип A	ВВГнг(A)-LS 3×2,5	18	0,4	1

Примечания

1. Схема однолинейная: одна линия — фаза, N и PE группы; аппараты — в отключённом положении (ГОСТ 2.702, ГОСТ 2.755). Номера групп — как у точек на планах (гр.). За отметку 0,000 принят уровень чистого пола; высота щита — по плану розеток.
2. Розеточные и мокрые линии — через УЗО или дифавтомат с током утечки не более 30 мА (ПУЭ 7.1.79); в санузле выполнить ДСУП (ПУЭ 7.1.87–7.1.88).
3. УЗО тип A — для линий с электроникой, стиральной и посудомоечной машиной, LED-драйверами; тип AC — только для чисто активной нагрузки.
4. Кабель — медный, исполнение нг(A)-LS (ГОСТ 31565-2012); скрытая прокладка только горизонтально и вертикально, фактические трассы зафиксировать исполнительной схемой до закрытия отделкой.
5. Номинал автомата — не выше допустимого тока кабеля: 1,5 мм² — до 10 А, 2,5 мм² — до 16 А. Резерв щита — не менее 20 % модулей.
6. Расчёт нагрузок, токов КЗ, селективности и сечений — по проекту ЭОМ организации с допуском СРО; лист задаёт состав, расположение и группы.
7. УЗИП FV1 — после вводного автомата, проводник к шине PE — кратчайший, без петель. Шина PE щита соединяется с ГЗШ проводником ОСУП; к ГЗШ присоединяются трубы водопровода и отопления на вводе в квартиру (ПУЭ 7.1.87). Шины N и PE — раздельные, после разделения PEN не объединяются.
8. До подключения нагрузки — приёмо-сдаточные испытания с протоколом: сопротивление изоляции линий не менее 0,5 МОм, срабатывание УЗО по току и времени, непрерывность защитных проводников PE (ПУЭ, гл. 1.8).

Допущения и предложения на листе

Основа листа: планировка по обводу плана заказчика, не замерена (К-1); высота до плиты 2650 мм от чистого пола — решение автора (ИЗ-1); отметки плана потолков сдвинуты на -95 мм (+2.745 плана = низ плиты), не замерено (К-2); толщины стен приняты: наружные 260 мм, перегородки 130 мм (К-1); положение стен и проёмов — по брифу без обмера и плана БТИ (К-1); разрешённая мощность 10 кВт принята, ТУ не переданы (К-6); вентканалы приняты, в брифе не заданы (К-5); тип дома, перекрытие и несущие стены не известны — документов нет (К-3); плита электрическая — принята, в брифе не указано (К-6); система заземления TN-C-S принята, ТУ не переданы (К-6); число жильцов 2 принято, в брифе не указано (К-9); подрайон климата не задан — принят не северный (жилые от 2,5 м) (К-26).

Открытые вопросы и конфликты по листу: К-6, К-9, К-24.

См. лист открытых вопросов (лист 5, записи К-1, К-3, К-5, К-6, К-9; лист 6, записи К-24, К-26).

Изм.	Кол.уч	Лист	№ док.	Подп.	Дата
Разраб.		Кырлан А.С.			04.11.26
Пров.					
ГИП					
Н. контр.					
Утв.					

ГД-2026-020-АИ

Квартира 68 м², элитный модерн

Общая площадь 68,47* м² · * размеры приняты, не замерены (реестр — л. 5–7, К-1)

Дизайн-проект интерьера

Стадия	Лист	Листов
РП	28	105

Однолинейная схема щита

М б/м

Кырлан Александр Сергеевич

выпуск 04.11.2026 № 8be4ef4c81 · стр. 31 из 117

Однолинейная схема щита (продолжение)

Щит квартирный ЩК · гр. 11—20 из 20 · без масштаба

Продолжение однолинейной схемы щита ЩК, начало — лист 28

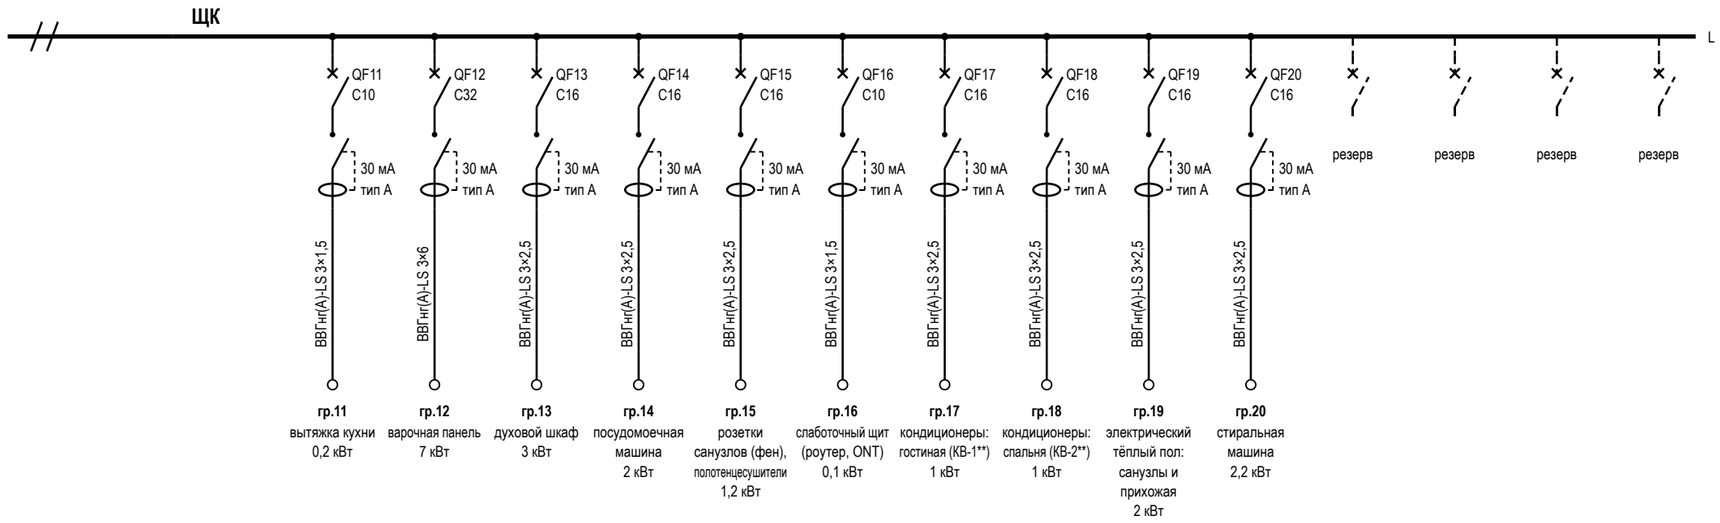


Таблица групп щита ЩК и кабельный журнал (продолжение)

№	Назначение	Помещения	Автомат	УЗО / дифавтомат	Кабель	Длина, м	Р, кВт	Точек
11	вытяжка кухни	5	C10	30 мА, тип A	ВВГнг(A)-LS 3×1,5	18	0,2	1
12	варочная панель	5	C32	30 мА, тип A	ВВГнг(A)-LS 3×6	18	7	1
13	духовой шкаф	5	C16	30 мА, тип A	ВВГнг(A)-LS 3×2,5	18	3	1
14	посудомоечная машина	5	C16	30 мА, тип A	ВВГнг(A)-LS 3×2,5	18	2	1
15	розетки санузлов (фен), полотенцесушители	2, 3	C16	30 мА, тип A	ВВГнг(A)-LS 3×2,5	27	1,2	2
16	слаботочный щит (роутер, ONT)	4	C10	30 мА, тип A	ВВГнг(A)-LS 3×1,5	6	0,1	6
17	кондиционеры: гостиная (КВ-1**)	6	C16	30 мА, тип A	ВВГнг(A)-LS 3×2,5	41	1	1
18	кондиционеры: спальня (КВ-2**)	7	C16	30 мА, тип A	ВВГнг(A)-LS 3×2,5	41	1	1
19	электрический тёплый пол: санузлы и прихожая	3, 4	C16	30 мА, тип A	ВВГнг(A)-LS 3×2,5	18,8	2	2
20	стиральная машина	3	C16	30 мА, тип A	ВВГнг(A)-LS 3×2,5	15	2,2	1
	Итого по сечениям ВВГнг(A)-LS (все группы щита), м: 3×1,5 — 145; 3×2,5 — 426,8; 3×6 — 18					589,8		

Примечания

1. Лист — продолжение однолинейной схемы щита ЩК: начало, данные щитка и условные обозначения — лист 28. Ввод, учёт, вводной аппарат, УЗИП, шины N и PE и ГЗШ показаны там же; шина L листа — та же шина щита.
2. Схема однолинейная: одна линия — фаза, N и PE группы; аппараты — в отключённом положении (ГОСТ 2.702, ГОСТ 2.755). Номера групп — как у точек на планах (гр.). За отметку 0,000 принят уровень чистого пола; высота щита — по плану розеток.
3. Розеточные и мокрые линии — через УЗО или дифавтомат с током утечки не более 30 мА (ПУЭ 7.1.79); в санузле выполнить ДСУП (ПУЭ 7.1.87–7.1.88).
4. УЗО тип A — для линий с электроникой, стиральной и посудомоечной машиной, LED-драйверами; тип AC — только для чисто активной нагрузки.
5. Кабель — медный, исполнение нг(A)-LS (ГОСТ 31565-2012); скрытая прокладка только горизонтально и вертикально, фактические трассы зафиксировать исполнительной схемой до закрытия отделкой.
6. Номинал автомата — не выше допустимого тока кабеля: 1,5 мм² — до 10 А, 2,5 мм² — до 16 А. Резерв щита — не менее 20 % модулей.
7. Расчёт нагрузок, токов КЗ, селективности и сечений — по проекту ЭОМ организации с допуском СРО; лист задаёт состав, расположение и группы.
8. До подключения нагрузки — приёмо-сдаточные испытания с протоколом: сопротивление изоляции линий не менее 0,5 МОм, срабатывание УЗО по току и времени, непрерывность защитных проводников PE (ПУЭ, гл. 1.8).

Допущения и предложения на листе

Основа листа: планировка по обводу плана заказчика, не замерена (К-1); высота до плиты 2650 мм от чистого пола — решение автора (ИЗ-1); отметки плана потолков сдвинуты на -95 мм (+2.745 плана = низ плиты), не замерено (К-2); толщины стен приняты: наружные 260 мм, перегородки 130 мм (К-1); положение стен и проёмов — по брифу без обмера и плана БТИ (К-1); разрешённая мощность 10 кВт принята, ТУ не переданы (К-6); вентканалы приняты, в брифе не заданы (К-5); тип дома, перекрытие и несущие стены не известны — документов нет (К-3); плита электрическая — принята, в брифе не указано (К-6); система заземления TN-C-S принята, ТУ не переданы (К-6); число жильцов 2 принято, в брифе не указано (К-9); подрайон климата не задан — принят не северный (жилые от 2,5 м) (К-26).


Знак «**» — предложение проектировщика, заказчиком не утверждено (согласовать с заказчиком): КВ-1, КВ-2 — кондиционер в жилой комнате — предложение по умолчанию (комфорт), заказчик может снять; модель, наружный блок, трасса фреона и дренаж — после обмера и согласования фасада.

См. лист открытых вопросов (лист 5, записи К-1, К-3, К-5, К-6, К-9; лист 6, запись К-26).

Изм.	Кол.уч	Лист	№ док.	Подп.	Дата	ГД-2026-020-АИ			
						Квартира 68 м², элитный модерн			
						Общая площадь 68,47* м² · * размеры приняты, не замерены (реестр — л. 5–7, К-1)			
Разраб.		Кырлан А.С.			04.11.26	Дизайн-проект интерьера	Стадия	Лист	Листов
Пров.							РП	29	105
ГИП									
Н. контр.						Однолинейная схема щита (продолжение) М б/м	Кырлан Александр Сергеевич		
Утв.									

План принципиальных трасс

Силовые трассы и объёмы электромонтажа, слаботочка в объёмах · размеры в мм

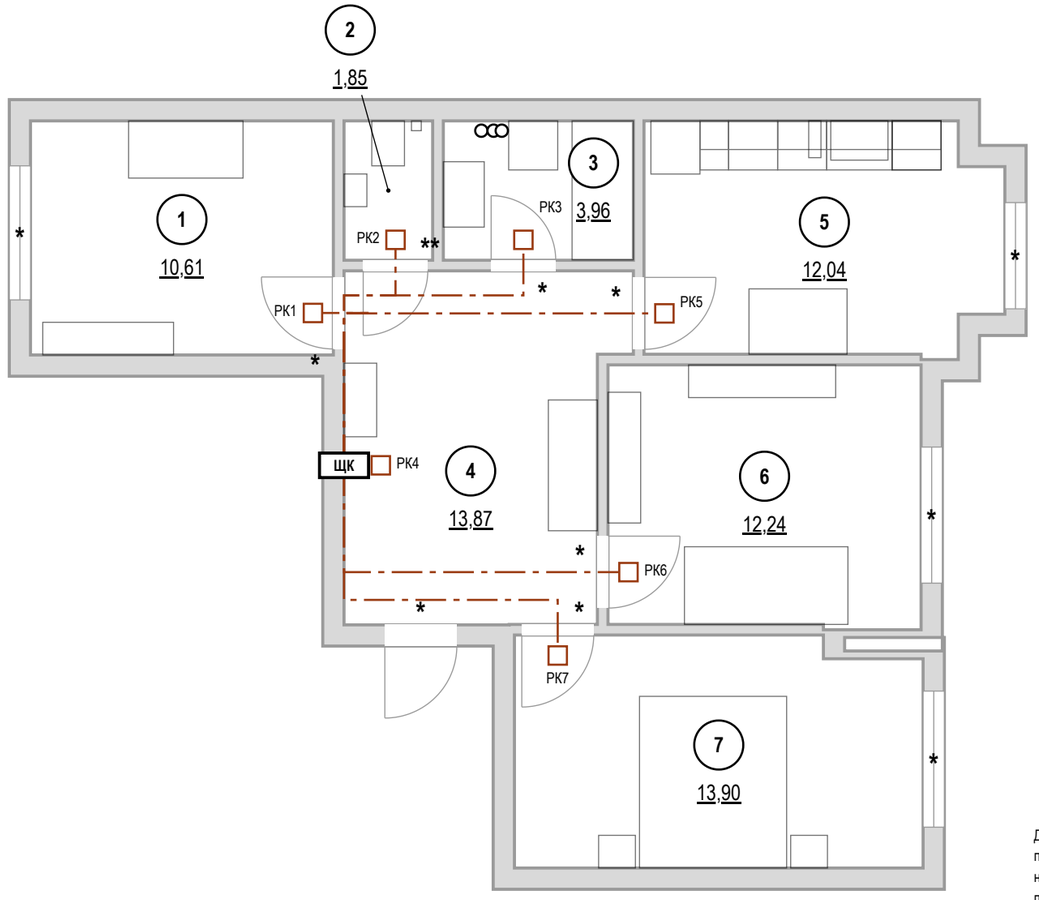

Кабель по группам ВВГнг(А)-LS, м

Гр.	мм²	Трасса	Данные
1	3×1,5	132,2	85
2	3×1,5	31,7	36
3	3×2,5	32	41
4	3×2,5	17,5	41
5	3×2,5	35,6	41
6	3×2,5	39,4	41
7	3×2,5	4,7	30
8	3×2,5	28,5	18
9	3×2,5	16	18
10	3×2,5	10,8	18

Гр.	мм²	Трасса	Данные
11	3×1,5	11,7	18
12	3×6	14,4	18
13	3×2,5	14,4	18
14	3×2,5	16,5	18
15	3×2,5	18,6	27
16	3×1,5	22,3	6
17	3×2,5	10,6	41
18	3×2,5	8,5	41
19	3×2,5	18,8	
20	3×2,5	14,4	15
Σ		**498,6**	**571**

Объёмы прокладки

Работа, материал	Ед.	Кол.
Гофротруба Ø20 в потолочном пространстве	м	210,6
Кабель-канал плинтуса для силовых линий	м	122,1
Короб или накладной канал для вертикальных спусков и подъёмов	м	85,9
Коробка распределительная (РК) над дверью помещения	шт	7
Слаботочка: кабель домофона	м	3,1
Слаботочка: Кабель коаксиальный RG-6 (75 Ом) к розеткам ТВ	м	14,1
Слаботочка: Кабель U/UTP кат. 5е (LAN, Wi-Fi и камеры по PoE)	м	27,4
Слаботочка: U/UTP кат. 6 (LAN, Wi-Fi, камеры)	м	2,7
Слаботочка: гофротруба Ø20 отдельно от силовых	м	42,6

Экспликация помещений

№	Помещение	Площадь, м²
1	Кабинет	10,61
2	Санузел	1,85
3	Ванная	3,96
4	Прихожая	13,87
5	Кухня-столовая	12,04
6	Гостиная	12,24
7	Спальня	13,90
	Итого (общая площадь)	68,47

Штробы — только после заключения

Работа	Ед.	Кол.
Вертикальные штробы 20×20 мм от потолка до каждой настенной точки (в маршрут без штроб не входят)	м	119,2

Условные обозначения

- ЩК — щит квартирный
- РК — распределительная коробка над дверью помещения
- магистраль от щита к РК: потолочное пространство, гофра
- мебель и сантехприборы — подложка

Допущения и предложения на листе. Основа листа: планировка по обводу плана заказчика, не замерена (К-1); высота до плиты 2650 мм от чистого пола — решение автора (ИЗ-1); отметки плана потолков сдвинуты на -95 мм (+2.745 плана = низ плиты), не замерено (К-2); толщины стен приняты: наружные 260 мм, перегородки 130 мм (К-1); положение стен и проёмов — по брифу без обмера и плана БТИ (К-1); разрешённая мощность 10 кВт принята, ТУ не переданы (К-6); вентканалы приняты, в брифе не заданы (К-5); тип дома, перекрытие и несущие стены не известны — документов нет (К-3); плита электрическая — принята, в брифе не указано (К-6); система заземления TN-C-S принята, ТУ не переданы (К-6); число жильцов 2 принято, в брифе не указано (К-9); подрайон климата не задан — принят не северный (жилые от 2,5 м) (К-26). Знак «*» — принято, не замерено и не подтверждено (замерить на объекте): К-4: Ст К1-1, Ст В1-2, Ст Т3-3 — положение стояка снято с обвода плана, не замерено. Знак «**» — предложение проектировщика, заказчиком не утверждено (согласовать с заказчиком): ЩС — щит слаботочный: место и состав. См. лист открытых вопросов (лист 5, записи К-1, К-3–К-6, К-9; лист 6, запись К-26).

Примечания

1. За отметку 0,000 принят уровень чистого пола. Высоты Н — от чистого пола до оси изделия; привязки — от чистовой грани стены до оси механизма (у рамки на несколько постов — до оси рамки).
2. Розеточные и мокрые линии — через УЗО или дифавтомат с током утечки не более 30 мА (ПУЭ 7.1.79); в санузле выполнить ДСУП (ПУЭ 7.1.87–7.1.88).
3. Кабель — медный, исполнение нг(А)-LS (ГОСТ 31565-2012); скрытая прокладка только горизонтально и вертикально, фактические трассы зафиксировать исполнительной схемой до закрытия отделкой.
4. Расчёт нагрузок, токов КЗ, селективности и сечений — по проекту ЭОМ организации с допуском СРО; лист задаёт состав, расположение и группы.
5. Длины — по плану: от щита вверх в потолочное пространство, по дверям и коридору без захода в мокрые помещения к распределительной коробке над дверью, далее к точкам; вертикали считаются вниз и обратно (у последней точки цепочки — в один конец); запас 10 %. Трассы принципиальные: фактическую зафиксировать исполнительной схемой до закрытия отделкой.
6. Несущие стены не определены: штробы в стенах не выполнять. Маршрут проложен без штроб: горизонтали — за потолком в гофре (210,6 м) и в кабель-канале плинтуса (122,1 м), вертикали — в коробе или накладном канале (151,2 м кабеля). Точек: за потолком — 44, спуск из потолка — 12, по плинтусу — 26, плинтус и подъём 34.
7. Вариант со штробами — работа после технического заключения: 119,2 м вертикальных штроб от потолка до каждой настенной точки; условие — только после технического заключения: стена не несущая (или вертикальная штроба в несущей согласована конструктором), глубина и ширина 20–25 мм, не в зонах 0–2 ванной. Без заключения и согласования конструктора в смету и в график эта работа не входит.
8. В данных проекта (журнал щита) длины кабеля внесены оценкой (571 м), по трассам из геометрии — 499 м (-13 %): к закупке и в смету принимать длины по трассам, а оценку в данных проекта заменить.
9. Слаботочные сети: кабели и точки считаются по лучам от ЩС** (лист слаботочных сетей): 47 м, портов патч-панели и коммутатора не менее 3; из точек 1 предложения листа слаботочки, не подтверждённые заказчиком. Изделия — в ведомости изделий.

1000 мм · печать 1:1

Изм.	Кол.уч	Лист	№ док.	Подп.	Дата
Разраб.		Кырлан А.С.			04.11.26
Пров.					
ГИП					
Н. контр.					
Утв.					

ГД-2026-020-АИ

Квартира 68 м², элитный модерн

Общая площадь 68,47* м² · * размеры приняты, не замерены (реестр — л. 5–7, К-1)

Дизайн-проект интерьера

Стадия	Лист	Листов
РП	30	105

План принципиальных трасс

М 1:75


Кырлан Александр Сергеевич

выпуск 04.11.2026 № 8be4ef4c81 · стр. 33 из 117

План слаботочных сетей

Интернет, ТВ, домофон · размеры в мм · высоты от чистого пола

ПРЕДВАРИТЕЛЬНО · не для производства работ · открыто пунктов: 25 (реестр — л. 5–7)

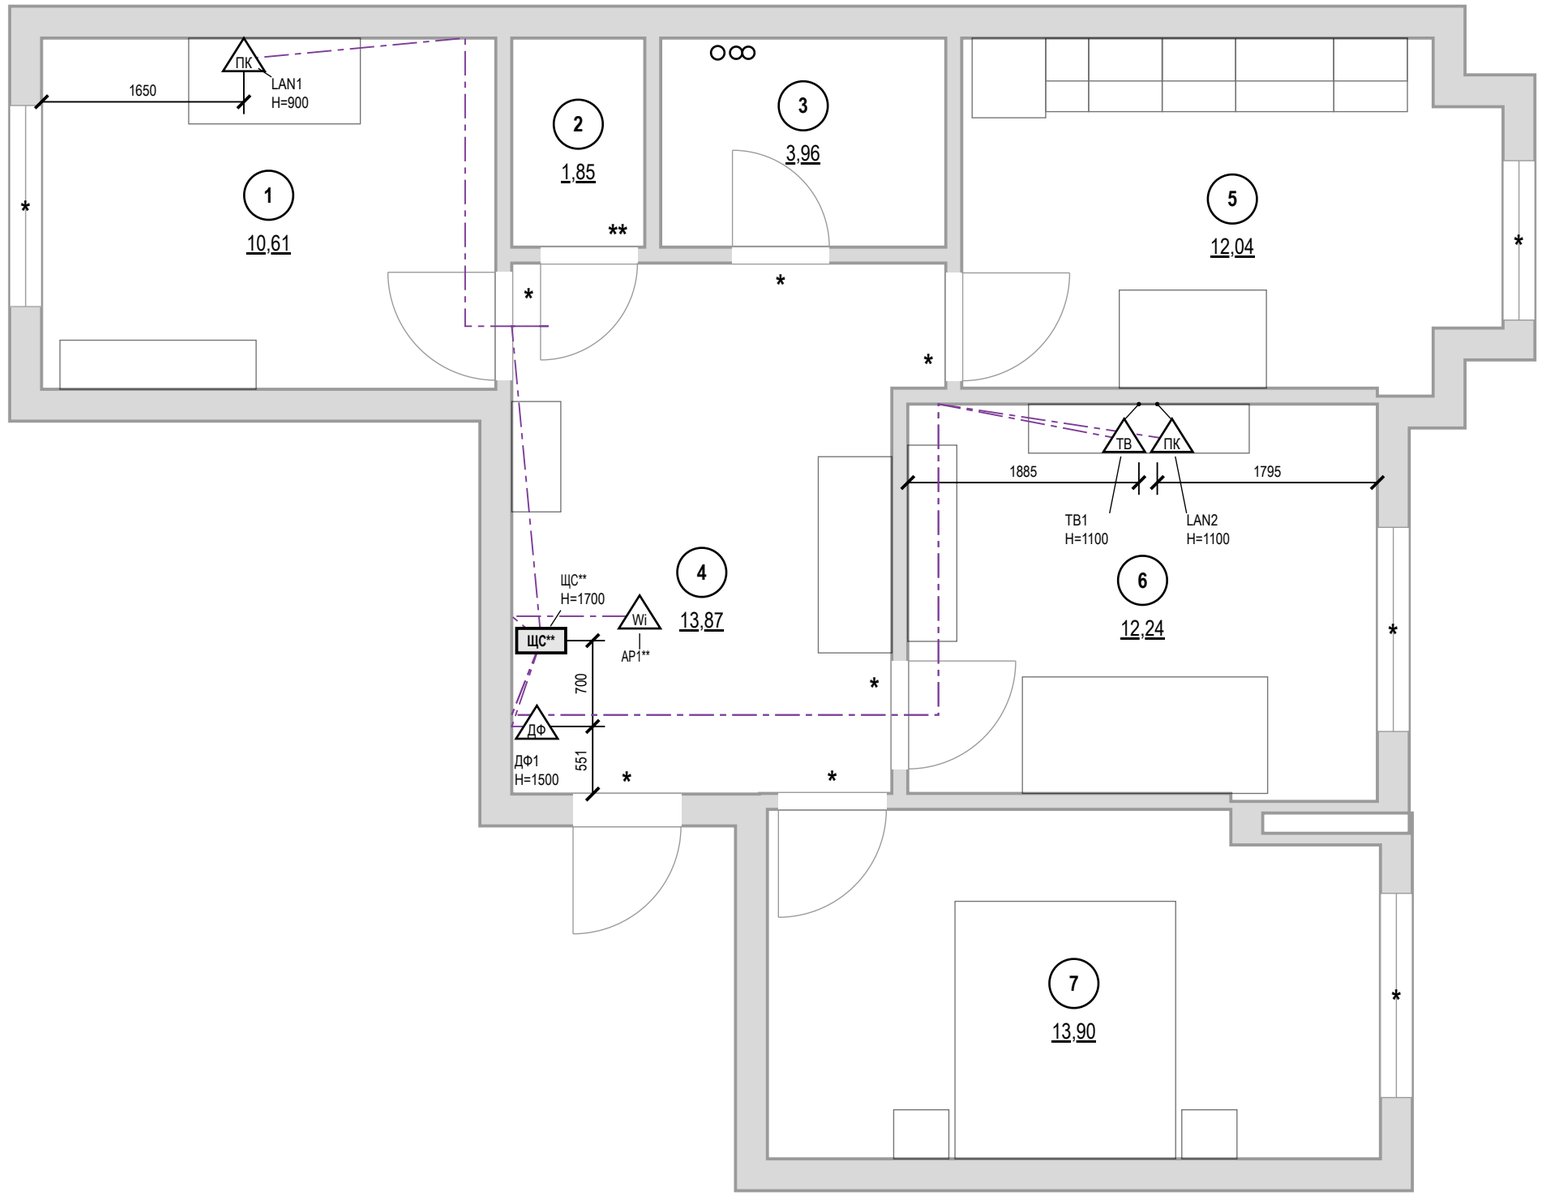

Ведомость слаботочных точек

Марка	Пом.	Назначение	H, мм	Кабель
LAN1	1	розетка LAN (RJ45)	900	U/UTP кат. 5e/6
ЩС**	4	щит слаботочный	1700	ввод пров.
ДФ1	4	домофон (трубка)	1500	по системе
AP1**	4	точка доступа Wi-Fi		U/UTP кат. 6 (PoE)
TB1	6	розетка ТВ	1100	RG-6 (75 Ом)
LAN2	6	розетка LAN (RJ45)	1100	U/UTP кат. 5e/6

Условные обозначения

- ЩС — щит слаботочный: ввод провайдера, роутер, коммутатор
- ПК — розетка компьютерная RJ45
- ТВ — розетка телевизионная
- ДФ — трубка или монитор домофона
- Wi — точка доступа Wi-Fi (питание PoE)
- кабель от ЩС до точки, отдельным лучом
- мебель и сантехприборы — подложка
- стояк: К1 — канализация, В1 — ХВС, Т3 — ГВС
- 1 — номер помещения, площадь м²

Допущения и предложения на листе. Основа листа: планировка по обводу плана заказчика, не замерена (К-1); высота до плиты 2650 мм от чистого пола — решение автора (ИЗ-1); отметки плана потолков сдвинуты на -95 мм (+2.745 плана = низ плиты), не замерено (К-2); толщины стен приняты: наружные 260 мм, перегородки 130 мм (К-1); положение стен и проёмов — по брифу без обмера и плана БТИ (К-1); разрешённая мощность 10 кВт принята, ТУ не переданы (К-6); вентканалы приняты, в брифе не заданы (К-5); тип дома, перекрытие и несущие стены не известны — документов нет (К-3); плита электрическая — принята, в брифе не указано (К-6); система заземления TN-C-S принята, ТУ не переданы (К-6); число жильцов 2 принято, в брифе не указано (К-9); подрайон климата не задан — принят не северный (жилые от 2,5 м) (К-26). Знак «*» — принято, не замерено и не подтверждено (замерить на объекте): К-4: Ст К1-1, Ст В1-2, Ст Т3-3 — положение стояка снято с обвода плана, не замерено. Знак «**» — предложение проектировщика, заказчиком не утверждено (согласовать с заказчиком): ЩС — щит слаботочный: место и состав; AP1 — точка доступа Wi-Fi: число и места. См. лист открытых вопросов (лист 5, записи К-1, К-3–К-6, К-9; лист 6, запись К-26).

Примечания

1. За отметку 0,000 принят уровень чистого пола. Высоты H — от чистого пола до оси изделия; привязки — от чистовой грани стены до оси механизма (у рамки на несколько постов — до оси рамки).
2. Высота установки, не указанная на плане: розетки LAN и ТВ — 300 мм от чистого пола.
3. Слаботочные кабели — отдельно от силовых: в своей трубе или лотке, при параллельной прокладке не ближе 100 мм к силовым, пересечения под прямым углом; каждую точку — отдельным кабелем от ЩС** без скруток.
4. Трассы на листе — принципиальные; фактические зафиксировать исполнительной схемой до закрытия отделкой. Силовые линии, УЗО 30 мА, ДСУП, кабель нг(A)-LS — по листам розеток и щита.
5. Проект силовой части и расчёт токов КЗ — по проекту ЭОМ; слаботочная часть согласуется с провайдером и управляющей компанией (домофон, коллективное ТВ).

1000 мм · печать 1:1

Изм.	Кол.уч	Лист	№ док.	Подп.	Дата
Разраб.		Кырлан А.С.			04.11.26
Пров.					
ГИП					
Н. контр.					
Утв.					

ГД-2026-020-АИ

Квартира 68 м², элитный модерн

Общая площадь 68,47* м² · * размеры приняты, не замерены (реестр — л. 5–7, К-1)

Дизайн-проект интерьера

Стадия	Лист	Листов
РП	31	105

План слаботочных сетей

М 1:50

Кырлан Александр Сергеевич

выпуск 04.11.2026 № 8be4ef4c81 · стр. 34 из 117

04

Отопление и вентиляция


Кырлан Александр Сергеевич

выпуск 04.11.2026 · № 8be4ef4c81 · стр. 35 из 117

План вентиляции

Вытяжка, приток, переток, кондиционеры · размеры в мм · высоты от чистого пола

ПРЕДВАРИТЕЛЬНО · не для производства работ · открыто пунктов: 25 (реестр — л. 5–7)

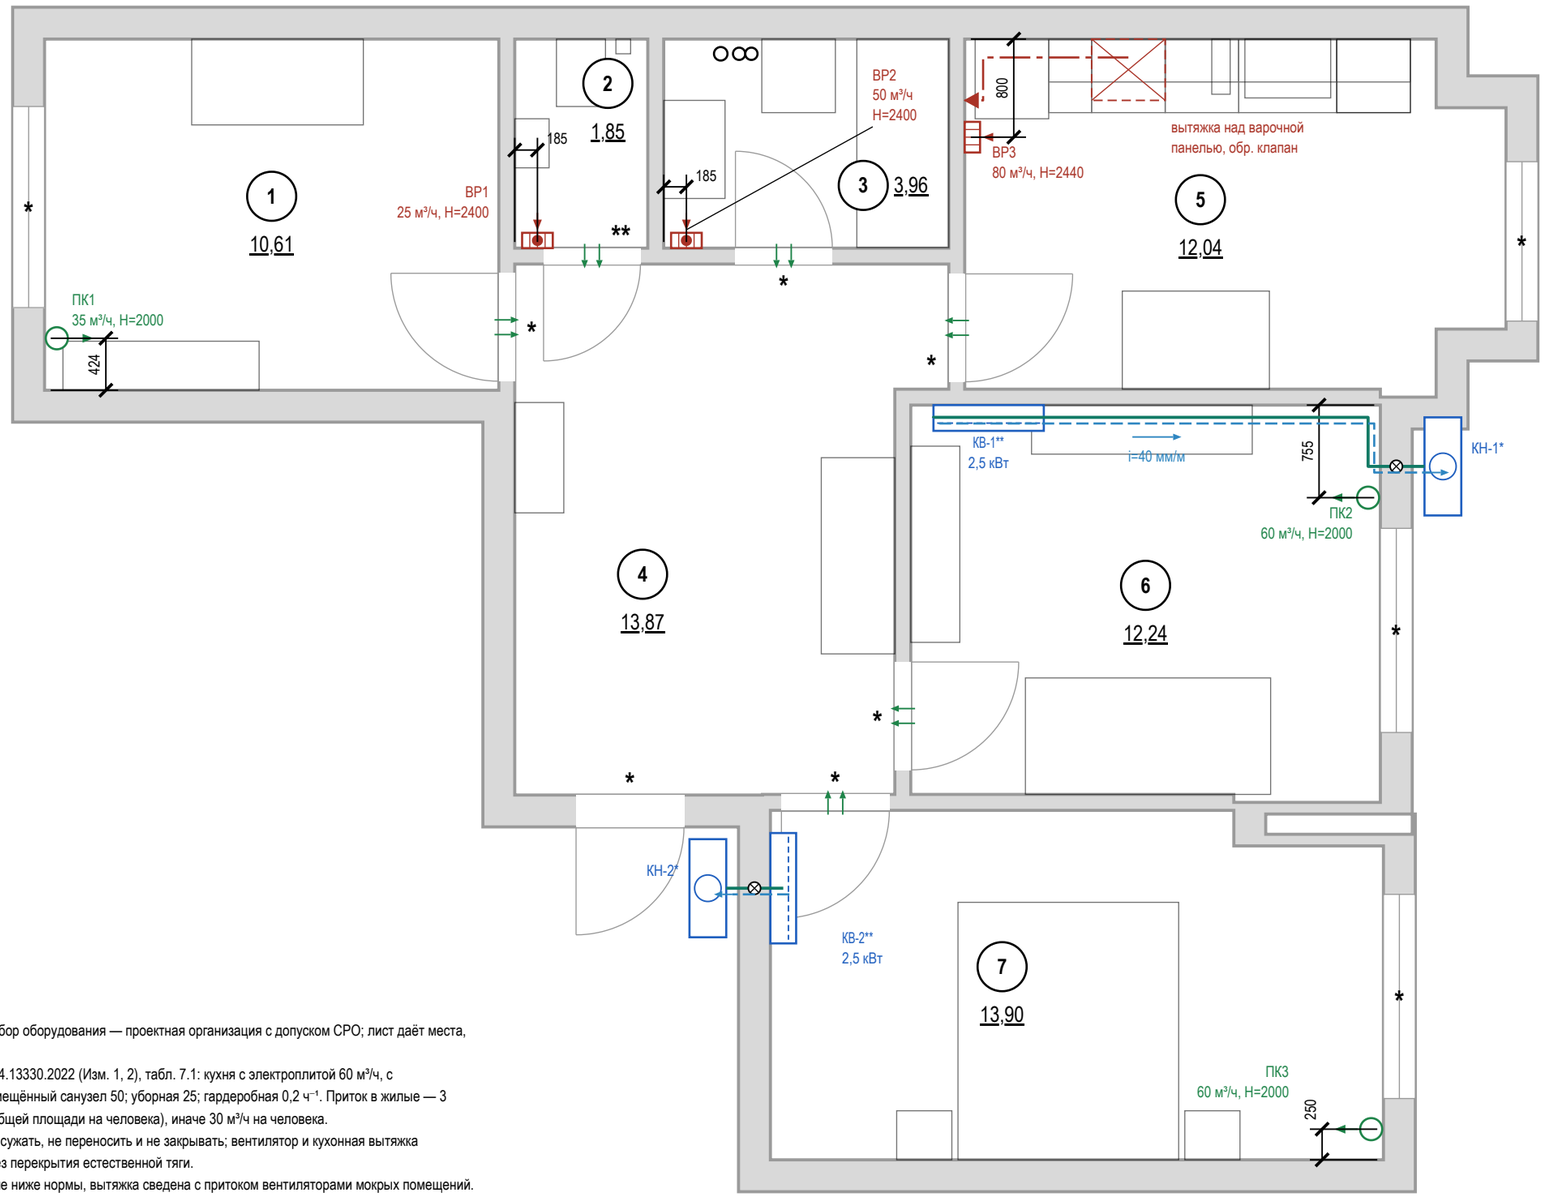

Условные обозначения

- стояк: К1 — канализация, В1 — ХВС, Т3 — ГВС
- номер помещения, площадь м²
- вытяжная решётка в вентканал: марка, расход м³/ч, Н центра от чистого пола
- вытяжная решётка с бытовым вентилятором и обратным клапаном: марка, расход, Н
- приточный клапан (КИВ) в наружной стене: марка, расход, Н центра
- переток: зазор под полотном или переточная решётка
- кухонная вытяжка над варочной панелью
- воздуховод кухонной вытяжки в коробе под потолком
- отдельный вход воздуховода в вентканал, обратный клапан
- внутренний блок кондиционера (КВ-N)
- наружный блок (КН-N) на фасаде / в корзине
- трасса фреонопровода и межблочного кабеля
- дренаж конденсата (уклон стрелкой)
- отверстие в наружной стене под трассу
- * — «*» — принято, не замерено и не подтверждено
- ** — «**» — предложение проектировщика, заказчиком не утверждено

Воздухообмен, м³/ч

№	Помещение	Выт. норма	Выт. проект	Прит. норма	Прит. проект	Устрой-ства
1	Кабинет			32	35	ПК1
2	Санузел	25	25			ВР1
3	Ванная	50	50			ВР2
5	Кухня-столовая	60	60			ВР3
6	Гостиная			60	60	ПК2
7	Спальня			60	60	ПК3
	Итого	**135**	**135**	**152**	**155**	
	Норма по жильцам: 30×2			60		

Воздухообмен квартиры — по большей из сумм притока и вытяжки: норма 152 м³/ч, проект 155 м³/ч.
Приток больше вытяжки на 20 м³/ч — поднять вытяжку.

Кондиционеры

Марка	Помещение	Нар. блок	Трасса, м	Дренаж
КВ-1**	6. Гостиная	КН-1*	4,7	наружу, i=40 мм/м
КВ-2**	7. Спальня	КН-2*	0,8	наружу, i=40 мм/м

Примечания

1. Расчёт систем ОВ и подбор оборудования — проектная организация с допуском СРО; лист даёт места, трассы и привязки.
2. Нормы вытяжки — СП 54.13330.2022 (Изм. 1, 2), табл. 7.1: кухня с электроплитой 60 м³/ч, с газовой 100; ванная и совмещённый санузел 50; уборная 25; гардеробная 0,2 ч⁻¹. Приток в жилые — 3 м³/ч на 1 м² (менее 20 м² общей площади на человека), иначе 30 м³/ч на человека.
3. Вентканалы и шахты не сужать, не переносить и не закрывать; вентилятор и кухонная вытяжка через обратный клапан, без перекрытия естественной тяги.
4. Проектные расходы — не ниже нормы, вытяжка сведена с притоком вентиляторами мокрых помещений. Клапаны — в простенке у окна, центр 2000 мм, не над кроватью, не ближе 300 мм к стоякам отопления; типоразмер — на расход.
5. Кухонная вытяжка в воздухообмен не включена: воздуховод не менее Ø125 в коробе, вход в канал отдельный.
6. Переток — зазор под полотнами межкомнатных дверей или переточная решётка.
7. Дренаж кондиционера — непрерывный уклон 40–60 мм/м без контруклонов (СТО НОСТРОЙ 2.23.1-2011, п. 5.8.4); врезка в К1 — через сифон (п. 5.8.9); длина трассы и перепад высот — по паспорту блока; внутренний блок — не ближе 150 мм к потолку, не над кроватью и рабочим местом.
8. Наружный блок на фасаде многоквартирного дома — с согласия собственников (общее имущество); при наличии корзин — только в них. Блоки со * размещены условно.
9. Привязки оборудования — по паспортам приобретённых моделей, до черновых работ.
10. Знак «*» у проёма — допущение: положение проёма не замерено (окно пом. 1, стена Г; дверь пом. 1, стена Б; дверь пом. 3, стена В; дверь пом. 4, стена В; окно пом. 5, стена Б; дверь пом. 5, стена Г; и ещё 4); размер напечатан как принятый. Реестр: листы 5–7, вопросы К-1, К-28.
11. Клапаны ПК1, ПК2, ПК3 выведены в простенок у окна, положение которого — допущение (знак «*»): после обмера окна привязку сверить.

1000 мм · печать 1:1

Допущения и предложения на листе. Основа листа: планировка по обводу плана заказчика, не замерена (К-1); высота до плиты 2650 мм от чистого пола — решение автора (ИЗ-1); отметки плана потолков сдвинуты на -95 мм (+2.745 плана = низ плиты), не замерено (К-2); толщины стен приняты: наружные 260 мм, перегородки 130 мм (К-1); положение стен и проёмов — по брифу без обмера и плана БТИ (К-1); разрешённая мощность 10 кВт принята, ТУ не переданы (К-6); вентканалы приняты, в брифе не заданы (К-5); тип дома, перекрытие и несущие стены не известны — документов нет (К-3); плита электрическая — принята, в брифе не указано (К-6); система заземления TN-C-S принята, ТУ не переданы (К-6); число жильцов 2 принято, в брифе не указано (К-9); подрайон климата не задан — принят не северный (жилые от 2,5 м) (К-26). Знак «*» — принято, не замерено (замерить): К-4: Ст К1-1, Ст В1-2, Ст Т3-3. Знак «**» — предложено, не утверждено (согласовать): КВ-1, КВ-2. См. лист открытых вопросов (лист 5, записи К-1, К-3–К-6, К-9; лист 6, запись К-26).

Изм.	Кол.уч	Лист	№ док.	Подп.	Дата
Разраб.		Кырлан А.С.			04.11.26
Пров.					
ГИП					
Н. контр.					
Утв.					

ГД-2026-020-АИ

Квартира 68 м², элитный модерн

Общая площадь 68,47* м² · * размеры приняты, не замерены (реестр — л. 5–7, К-1)

Привязки — до обмера

Вентканалы и исходные данные не заданы. Решётки и вход вытяжки показаны у стояков К1 (вентблоку мокрой зоны). До черновых работ — обмер каналов и проверка тяги; лист перевыпустить по факту.

Дизайн-проект интерьера

Стадия	Лист	Листов
РП	32	105

План вентиляции

М 1:50


Кырлан Александр Сергеевич

выпуск 04.11.2026 № 8be4ef4c81 · стр. 36 из 117

План отопления

Радиаторы, стояки, подводки · размеры в мм · высоты от чистого пола

ПРЕДВАРИТЕЛЬНО · не для производства работ · открыто пунктов: 25 (реестр — л. 5–7)

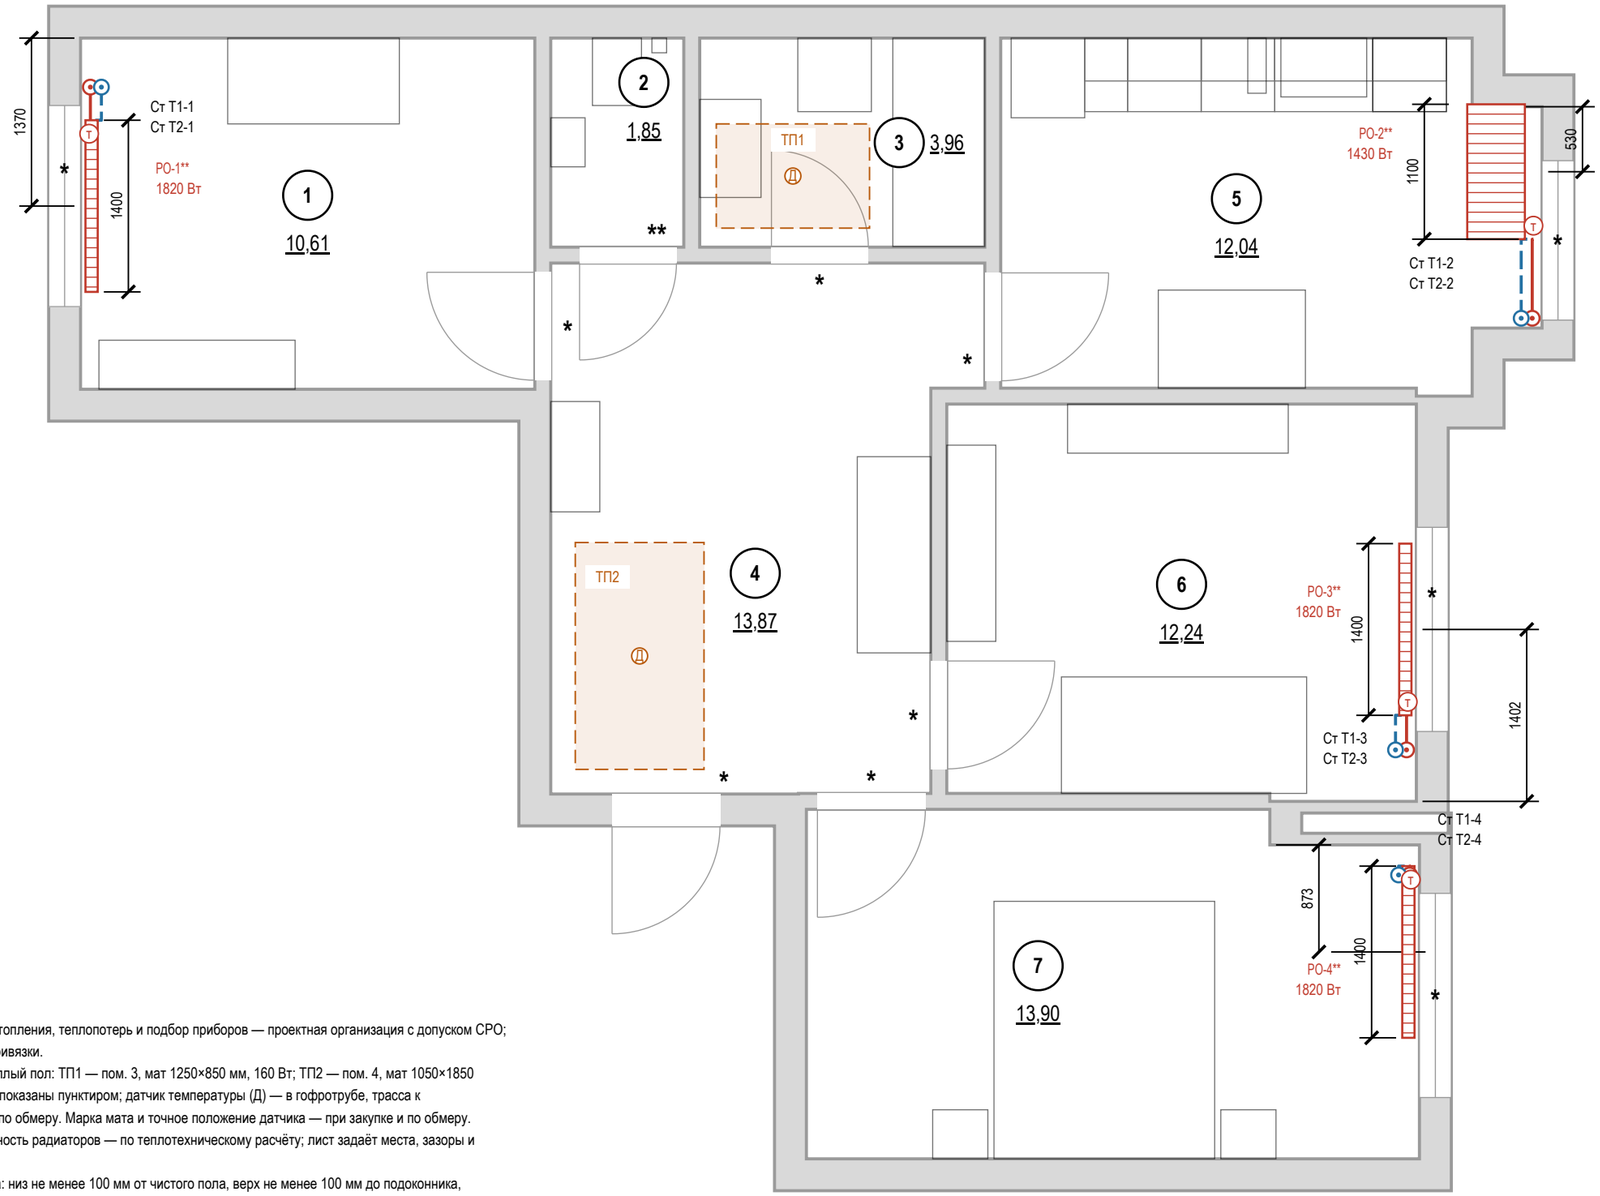

Условные обозначения

- (1) — номер помещения, площадь м²
- радиатор отопления (марка РО-N, длина по плану)
- (Т) — клапан с термоголовкой на подаче
- стояк отопления, подающий (Ст Т1-N)
- стояк отопления, обратный (Ст Т2-N)
- Т1 — отопление, подающий трубопровод
- Т2 — отопление, обратный трубопровод
- * — «*» — принято, не замерено и не подтверждено
- ** — «**» — предложение проектировщика, заказчиком не утверждено

Ведомость радиаторов

Марка	Помещение	Тип	Д×В×Г, мм	Низ / стена	Q, Вт
РО-1**	1. Кабинет	панельный 22	1400×500×100	120 / 40	1820
РО-2**	5. Кухня-столовая	панельный 22	1100×500×100	120 / 40	1430
РО-3**	6. Гостиная	панельный 22	1400×500×100	120 / 40	1820
РО-4**	7. Спальня	панельный 22	1400×500×100	120 / 40	1820

Низ — от чистого пола, стена — зазор до задней панели, мм.

Привязки — до обмера

Стояки отопления в исходных данных не заданы: показаны у откосов окон, подводки — принципиально. До черновых работ — обмер стояков и паспорта приборов; лист перевыпустить по факту.

Примечания

1. Расчёт системы отопления, теплопотерь и подбор приборов — проектная организация с допуском СРО; лист даёт места и привязки.
2. Электрический тёплый пол: ТП1 — пом. 3, мат 1250×850 мм, 160 Вт; ТП2 — пом. 4, мат 1050×1850 мм, 290 Вт; контуры показаны пунктиром; датчик температуры (Д) — в гофротрубе, трасса к терморегулятору — по обмеру. Марка мата и точное положение датчика — при закупке и по обмеру.
3. Тип, длина и мощность радиаторов — по теплотехническому расчёту; лист задаёт места, зазоры и подключение.
4. Зазоры радиатора: низ не менее 100 мм от чистого пола, верх не менее 100 мм до подоконника, 30–50 мм от стены до задней панели; центр по оси окна с допуском ±20 мм. Верх до подоконника — 280 мм.
5. Радиаторы не закрывать глухими коробами и мебелью; перенос и замена приборов в многоквартирном доме — переустройство, согласование с управляющей организацией (ЖК РФ ст. 25–26); вынос на лоджию запрещён.
6. Трубы отопления через межквартирные стены не прокладывать (СП 51.13330.2011, п. 9.19); через перекрытия и перегородки — в гильзах.
7. Привязки приборов и подводок — по паспортам приобретённых радиаторов и клапанов, до черновых работ.
8. До закрытия отделкой трубопроводы отопления испытать гидростатическим давлением с оформлением акта (СП 73.13330.2016, 7.2–7.3).
9. Знак «*» у проёма — допущение: положение проёма не замерено (окно пом. 1, стена Г; дверь пом. 1, стена Б; дверь пом. 3, стена В; дверь пом. 4, стена В; окно пом. 5, стена Б; дверь пом. 5, стена Г; и ещё 4); размер напечатан как принятый. Реестр: листы 5–7, вопросы К-1, К-28.
10. Радиаторы РО-1**, РО-2**, РО-3**, РО-4** стоят по оси окна, положение которого — допущение (знак «*»): после обмера окна привязки приборов и подводок сверить.

1000 мм · печать 1:1

Допущения и предложения на листе. Основа листа: планировка по обводу плана заказчика, не замерена (К-1); высота до плиты 2650 мм от чистого пола — решение автора (ИЗ-1); отметки плана потолков сдвинуты на -95 мм (+2.745 плана = низ плиты), не замерено (К-2); толщины стен приняты: наружные 260 мм, перегородки 130 мм (К-1); положение стен и проёмов — по брифу без обмера и плана БТИ (К-1); разрешённая мощность 10 кВт принята, ТУ не переданы (К-6); вентканалы приняты, в брифе не заданы (К-5); тип дома, перекрытие и несущие стены не известны — документов нет (К-3); плита электрическая — принята, в брифе не указано (К-6); система заземления TN-C-S принята, ТУ не переданы (К-6); число жильцов 2 принято, в брифе не указано (К-9); подрайон климата не задан — принят не северный (жилые от 2,5 м) (К-26). Знак «*» — принято, не замерено (замерить). Знак «**» — предложено, не утверждено (согласовать): РО-1, РО-2, РО-3, РО-4. См. лист открытых вопросов (лист 5, записи К-1, К-3, К-5, К-6, К-9; лист 6, запись К-26).

Изм.	Кол.уч	Лист	№ док.	Подп.	Дата
Разраб.		Кырлан А.С.			04.11.26
Пров.					
ГИП					
Н. контр.					
Утв.					

ГД-2026-020-АИ

Квартира 68 м², элитный модерн

Общая площадь 68,47* м² · * размеры приняты, не замерены (реестр — л. 5–7, К-1)

Дизайн-проект интерьера

Стадия	Лист	Листов
РП	33	105

План отопления

М 1:50

Кырлан Александр Сергеевич

выпуск 04.11.2026 № 8be4ef4c81 · стр. 37 из 117

05

Водоснабжение и канализация

Кырлан Александр Сергеевич

выпуск 04.11.2026 № 8be4ef4c81 · стр. 38 из 117


План выводов сантехники

Выводы В1, Т3, К1 · привязки от чистовых стен · высоты от чистого пола, мм


ПРЕДВАРИТЕЛЬНО · не для производства работ · открыто пунктов: 25 (реестр — л. 5–7)

Допущения и предложения на листе. Знак «*» принято (замерить). Знак «**» предложено (согласовать). См. лист открытых вопросов (листы 5–7).


Фрагмент 1. Санузел (пом. 2)

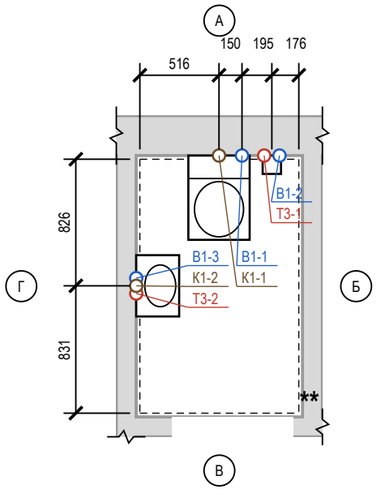

Фрагмент 2. Ванная (пом. 3)

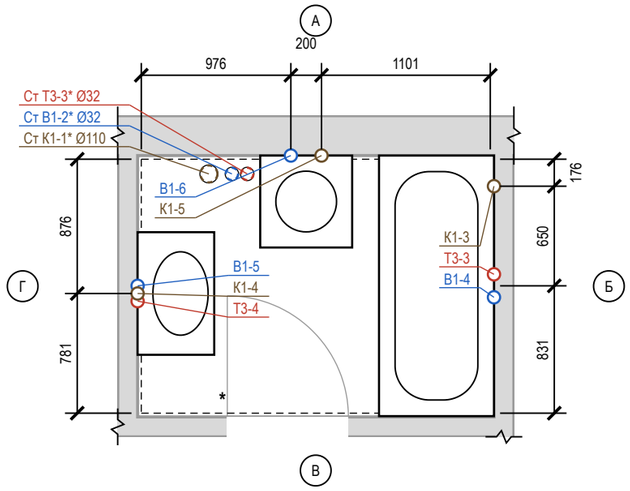

Фрагмент 3. Кухня-столовая (пом. 5)

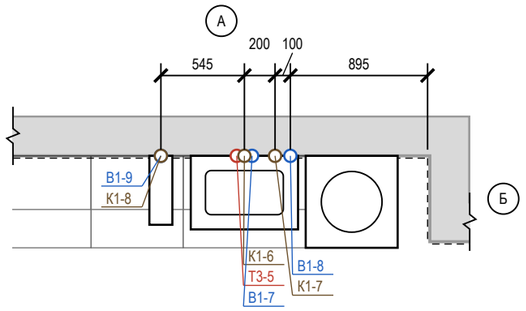

Ведомость привязок выводов

Код	Прибор	Ø	Н, мм	Привязка от чист. стен, мм	Прим.
В1-1	П4 унитаз подвесной	½"	1000	ст. А: 371 от Б	в раме инсталляции
К1-1	П4 унитаз подвесной	Ø110	220	ст. А: 516 от Г	
В1-2	П5** гигиенический душ	½"	750	ст. А: 126 от Б	межос. 100
Т3-1	П5** гигиенический душ	½"	750	ст. А: 226 от Б	межос. 100
В1-3	П7 умывальник	½"	550	ст. Г: 776 от А	межос. 100
Т3-2	П7 умывальник	½"	550	ст. Г: 781 от В	межос. 100
К1-2	П7 умывальник	Ø40	500	ст. Г: 826 от А	
В1-4	П9** ванна	½"	800	ст. Б: 756 от В	межос. 150
Т3-3	П9** ванна	½"	800	ст. Б: 751 от А	межос. 150
К1-3	П9** ванна	Ø50	50	ст. Б: 176 от А	
В1-5	П10** умывальник	½"	550	ст. Г: 826 от А	межос. 100
Т3-4	П10** умывальник	½"	550	ст. Г: 731 от В	межос. 100
К1-4	П10** умывальник	Ø40	500	ст. Г: 781 от В	
В1-6	П16** стиральная машина	½"	600	ст. А: 976 от Г	кран машины
К1-5	П16** стиральная машина	Ø40	600	ст. А: 1101 от Б	
В1-7	П1 мойка кухонная	½"	600	ст. А: 1145 от Б	межос. 100
Т3-5	П1 мойка кухонная	½"	600	ст. А: 1245 от Б	межос. 100
К1-6	П1 мойка кухонная	Ø50	400	ст. А: 1195 от Б	
В1-8	П2 посудомоечная машина	½"	550	ст. А: 895 от Б	кран ПММ в шкафу мойки
К1-7	П2 посудомоечная машина	Ø40	550	ст. А: 995 от Б	слив ПММ в шкафу мойки
В1-9	П3** фильтр обратного осмоса	½"	550	ст. А: 1740 от Б	
К1-8	П3** фильтр обратного осмоса	Ø40	450	ст. А: 1740 от Б	

* — высота по практике монтажа; сверить по паспорту прибора

Условные обозначения

- вывод В1 (код — в ведомости привязок)
- вывод Т3 (код — в ведомости привязок)
- вывод К1 (код — в ведомости привязок)
- сантехприбор по расстановке (габарит модели)
- чистовая поверхность стены (от неё привязки)
- стояк «Ст К1-N / Ст В1-N» (ГОСТ 21.601), Ø мм
- * стояк Т3 не на обмере — принят в шахте рядом со Ст В1, сверить
- линия обрыва (граница фрагмента)
- А — обозначение стены А–Г (как на развёртках)

Примечания

1. Привязки выводов даны от чистовых поверхностей стен (облицовка на сторону: санузел — 24 мм (штукатурка 10 + клей 5 + плитка 9); ванная — 24 мм (штукатурка 10 + клей 5 + плитка 9); кухня-столовая — 24 мм (фартук: штукатурка 10 + клей 5 + плитка 9)); эти же грани — на развёртках и в раскладке плитки. Высоты — от чистого пола помещения.
2. Высоты и межосевые, отмеченные «*», приняты по практике монтажа; до черновой разводки сверить по паспорту выбранного прибора (смеситель, инсталляция, сифон).
3. Горячая вода (Т3) — слева от холодной (В1), если смотреть на прибор. Допуск установки выводов: ±5 мм в группе, ±20 мм у отдельно стоящих.
4. Расчёт систем водоснабжения и канализации и подбор оборудования выполняет проектная организация; лист задаёт места и высоты выводов.
5. Посудомоечная машина П2: кран и слив — отдельными выводами в шкафу мойки (не за машиной), до машины ≤ 1500 мм.
6. Ст К1-1*, Ст В1-2*, Ст Т3-3* на обмере не показаны: положение принято (исполнитель по плану заказчика), не замерено (К-4); положение сверить на объекте до разметки.
7. Стояки в коробах/шахтах не замоноличивать; стояк К1 в коробе — звукоизоляция стояка в коробе без жёсткого контакта с трубой; к арматуре и ревизиям — люк не меньше 300×400.

1000 мм · печать 1:1

Изм.	Кол.уч	Лист	№ док.	Подп.	Дата
Разраб.		Кырлан А.С.			04.11.26
Пров.					
ГИП					
Н. контр.					
Утв.					

ГД-2026-020-АИ

Квартира 68 м², элитный модерн

Общая площадь 68,47* м² · * размеры приняты, не замерены (реестр — л. 5–7, К-1)

Дизайн-проект интерьера

Стадия	Лист	Листов
РП	34	105

План выводов сантехники

М 1:40

Кырлан Александр Сергеевич


выпуск 04.11.2026 № 8be4ef4c81 · стр. 39 из 117

Схема разводки водопровода и канализации


Схемы систем В1, Т3, К1 · трассы принципиальные · уклоны в мм на 1 м · план М 1:200, фрагменты М 1:25

ПРЕДВАРИТЕЛЬНО · не для производства работ · открыто пунктов: 25 (реестр — л. 5–7)


План квартиры (М 1:200)

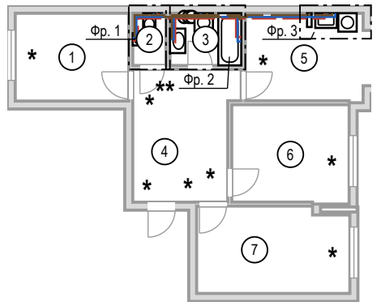


Фр. 3. Кухня-столовая (М 1:25)

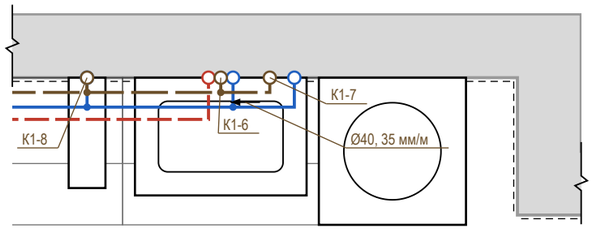

Фр. 1. Санузел (М 1:25)

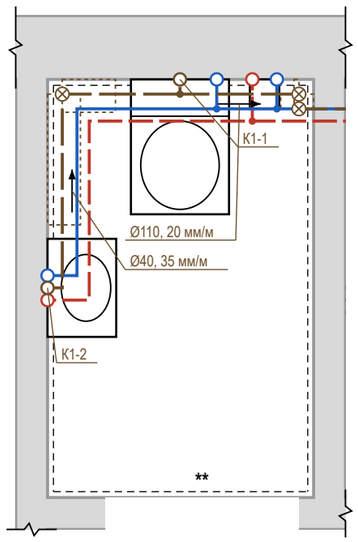

Фр. 2. Ванная (М 1:25)

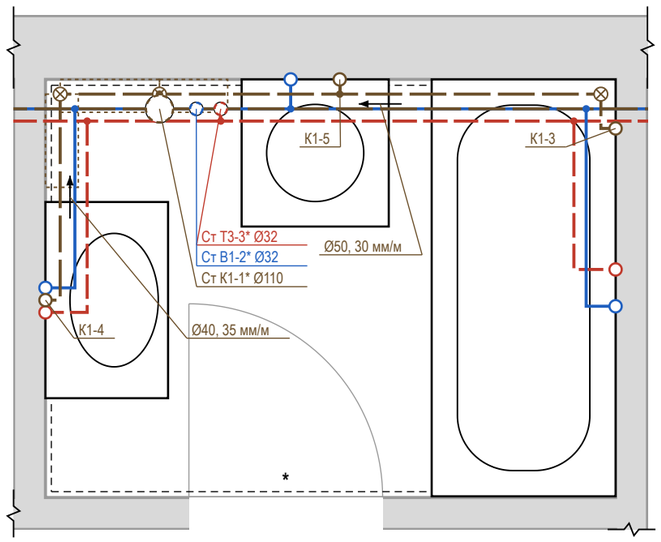

Условные обозначения


- В1 — водопровод хозяйственно-питьевой (ХВС), PP-R Ø20
- Т3 — горячее водоснабжение, подача (ГВС), PP-R Ø20
- К1 — канализация бытовая
- направление уклона К1 / пола: Ø, мм на 1 м
- ревизия (прочистка) К1 — доступ сохранить
- тройник (ответвление к прибору)
- короб К1 над чистым полом (ГКЛВ под плитку)
- вывод В1 (код — в ведомости привязок)
- вывод Т3 (код — в ведомости привязок)
- вывод К1 (код — в ведомости привязок)
- сантехприбор по расстановке (габарит модели)
- стояк «Ст К1-N / Ст В1-N» (ГОСТ 21.601), Ø мм
- * стояк Т3 не на обмере — принят в шахте рядом со Ст В1, сверить
- линия обрыва (граница фрагмента)
- граница фрагмента на плане (Фр. N)

Профиль выпусков К1 (до врезки в стояк)

Выпуск	Прибор	Ø	L, м	i, мм/м	Δh, мм	Прокладка, мм
К1-1	П4 унитаз подвесной	Ø110	1,26	20	25	в полу не помещается: 210 > 90; К-27
К1-6	П1 мойка кухонная	Ø50	4,75	30	142	над полом за приборами
К1-3	П9** ванна	Ø50	2,06	30	62	в полу не помещается: 187 > 90; К-28
К1-7	П2 посудомоечная машина	Ø40	4,95	35	173	над полом за приборами
К1-8	П3** фильтр обратного осмоса	Ø40	4,20	35	147	над полом за приборами
К1-2	П7 умывальник	Ø40	2,53	35	89	короб 160×110
К1-4	П10** умывальник	Ø40	1,36	35	48	короб 120×110
К1-5	П16** стиральная машина	Ø40	0,85	35	30	короб 100×110

Короб h×b: h — от чистого пола, b — от чистовой стены. Стяжка 90 мм — лист полов.

Узел ввода В1, Т3 (по данным, без масштаба)

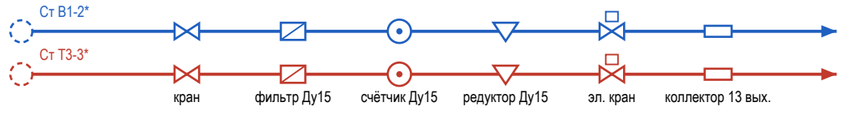

⊗ Ст К1-1*: ревизия на стояке — люк в коробе

Примечания

1. Трассы принципиальные, построены от стояков вдоль стен помещений; фактическое положение фиксируется исполнительной схемой с привязками (фото с рулеткой) до закрытия.
2. Уклон К1 не менее 1/d и не более 150 мм/м (СП 30.13330.2020, п. 19.1), приняты практические уклоны; поворот — двумя отводами 45°, ревизия после поворота, доступ сохранить. Стояк К1 в коробе — звукоизоляция стояка в коробе, без жёсткого контакта короба с трубой.
3. Решение по К1: стяжка 90 мм не укрывает трубы (нужно Ø + Δh + 45 мм) — выпуски идут над чистым полом вдоль стен: К1-6, К1-7, К1-8 — за приборами и в раме инсталляции; К1-2, К1-4, К1-5 — в коробе ГКЛВ под плитку (размеры в профиле). Короба — на развёртках; отметку низа врезки в стояк замерить до черновых работ.
4. К1-1 (П4 унитаз подвесной): Δh 25 + Ø110 + 45 = 210 мм > пирога 90 мм — в стяжке не помещается: подиум или подъём пола на 120 мм, короб 170×140 или прибор ближе к стояку — решение К-27; до решения не выполнять.
5. К1-3 (П9** ванна): Δh 62 + Ø50 + 45 = 187 мм > пирога 90 мм — в стяжке не помещается: подиум или подъём пола на 100 мм, короб 150×110 или прибор ближе к стояку — решение К-28, ИЗ-3, К-28; до решения не выполнять.
6. Отводы К1-6 (4,7 м), К1-7 (4,9 м), К1-8 (4,2 м) длиннее 4 м без вентиляции — у прибора воздушный клапан Ø50 в доступном месте (за люком или в тумбе) либо вентилируемый отвод (EN 12056-2, табл. 4); предложение проектировщика, подбор — проектная организация.
7. Узел ввода В1, Т3 — по данным проекта: кран → фильтр Ду15 → счётчик Ду15 → редуктор Ду15 → эл. кран → коллектор 13 вых.. Доступ к арматуре — через люк не меньше 300×400. Водопровод — в штробе стен или в коробах; трубы испытать давлением до закрытия (акт скрытых работ).
8. Расчёт систем, диаметры магистралей и подбор оборудования выполняет проектная организация; врезка и перенос стояков — по согласованию с управляющей организацией. Арматуру и привязки сверить по паспортам приборов.
9. Ст К1-1*, Ст В1-2*, Ст Т3-3* на обмере не показаны: положение принято (исполнитель по плану заказчика), не замерено (К-4); положение сверить на объекте до разводки.

Допущения и предложения на листе. Знак «*» принято (замерить): дверь пом. 3 (стена В). Знак «**» предложено (согласовать). См. лист открытых вопросов (листы 5–7).

Изм.	Кол.уч	Лист	№ док.	Подп.	Дата
Разраб.		Кырлан А.С.			04.11.26
Пров.					
ГИП					
Н. контр.					
Утв.					

ГД-2026-020-АИ

Квартира 68 м², элитный модерн

Общая площадь 68,47* м² · * размеры приняты, не замерены (реестр — л. 5–7, К-1)

Дизайн-проект интерьера

Стадия	Лист	Листов
РП	35	105

Схема разводки водопровода и канализации

М 1:200; 1:25

Кырлан Александр Сергеевич


выпуск 04.11.2026 № 8be4ef4c81 · стр. 40 из 117

Аксонометрическая схема В1 (холодное водоснабжение)

аксонометрия · диаметры, уклоны, отметки, стояки и приборы · трассы принципиальные

Схема В1 (М 1:50; по вертикали и горизонтали один масштаб, глубина — ×0,5 под 45°)

ПРЕДВАРИТЕЛЬНО · не для производства работ · открыто пунктов: 25 (реестр — л. 5–7)

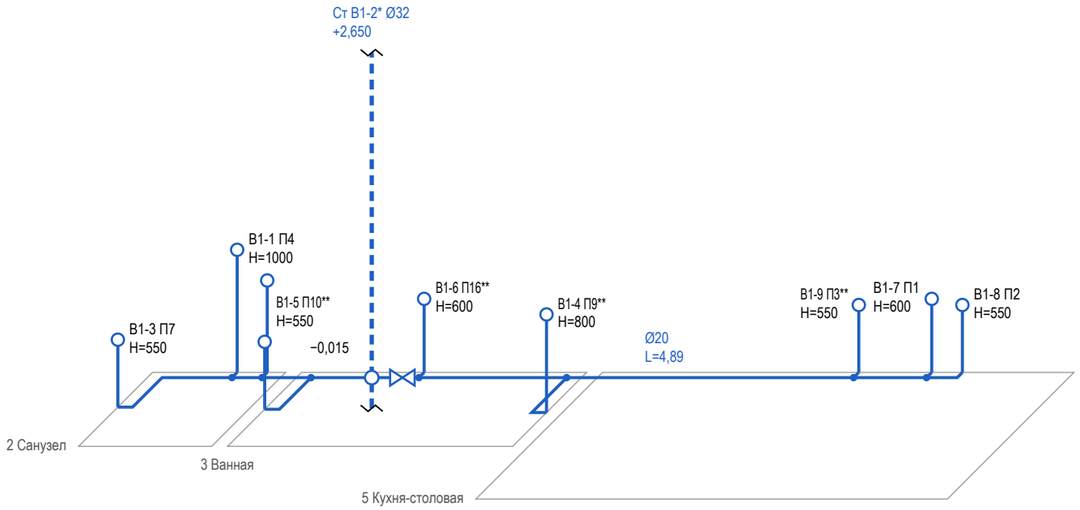

Условные обозначения

- В1 — водопровод хозяйственно-питьевой (ХВС), PP-R Ø20
- вывод В1 (код — в ведомости привязок)
- стояк «Ст К1-N / Ст В1-N» (ГОСТ 21.601), Ø мм
- стояк в плане (на отметке пола); вертикаль — стояк по высоте, разрыв — перекрытие
- тройник (ответвление к прибору)
- кран шаровой
- * стояк Т3 не на обмере — принят в шахте рядом со Ст В1, сверить

Допущения и предложения на листе

Основа листа: планировка по обводу плана заказчика, не замерена (К-1); высота до плиты 2650 мм от чистого пола — решение автора (ИЗ-1); отметки плана потолков сдвинуты на -95 мм (+2.745 плана = низ плиты), не замерено (К-2); толщины стен приняты: наружные 260 мм, перегородки 130 мм (К-1); положение стен и проёмов — по брифу без обмера и плана БТИ (К-1); разрешённая мощность 10 кВт принята, ТУ не переданы (К-6); вентканалы приняты, в брифе не заданы (К-5); тип дома, перекрытие и несущие стены не известны — документов нет (К-3); плита электрическая — принята, в брифе не указано (К-6); система заземления TN-C-S принята, ТУ не переданы (К-6); число жильцов 2 принято, в брифе не указано (К-9); подрайон климата не задан — принят не северный (жилые от 2,5 м) (К-26).

Знак «*» — принято, не замерено и не подтверждено (замерить на объекте): К-4: Ст В1-2, Ст К1-1, Ст Т3-3 — положение стояка снято с обвода плана, не замерено.

Знак «**» — предложение проектировщика, заказчиком не утверждено (согласовать с заказчиком): П3 — питьевая вода без бытового фильтра в доме не гарантирована; фильтр под мойкой — предложение по умолчанию, заказчик может снять (с дренажом отдельной врезкой); ИЗ-3, К-7: П10 — раковина у левой стены: светильники 14 плана — у зеркала над ней; отвод К1 к стояку в углу короткий; П16 — место стиральной машины — в ванной у верхней стены, правее короба стояка; подход 1100 мм перед дверцей, выводы ХВС и К1 Ø40 за машиной; ИЗ-3, К-28: П9 — ванна 1700 × 750 у правой стены на всю глубину помещения (1700 мм по плану) — стояк в левом углу свободен.

Открытые вопросы и конфликты по листу: К-29.

См. лист открытых вопросов (лист 5, записи К-1, К-3–К-7, К-9; лист 6, запись К-26; лист 7, записи ИЗ-3, К-28, К-29).

Примечания

1. Схема В1 построена по тем же трассам, что план разводки: положение в плане сохранено, глубина — в масштабе ×0,5. Трассы принципиальные; фактическое положение фиксируется исполнительной схемой до закрытия.
2. Высоты Н — от чистого пола помещения, мм. Прокладка магистрали В1 по данным: коллекторная разводка, в стяжке пола, в стяжке пола, выше плиты перекрытия; отметка трасс — по пирогу пола.
3. Узел ввода В1 (кран, фильтр, счётчик, обратный клапан, кран) — на схеме разводки; состав узла ввода — по согласованию. Кран шаровой — на первом участке от стояка.
4. Ст В1-2* на обмере не показаны: положение принято (исполнитель по плану заказчика), не замерено (К-4); положение сверить на объекте до разводки.
5. Трубы испытать давлением до закрытия (акт скрытых работ, опрессовка по СП 73.13330.2016).
6. Диаметры, высоты выводов и места кранов — по паспортам выбранных приборов и расчёту проектной организации.
7. Расчёт систем, диаметры магистралей и подбор оборудования выполняет проектная организация.

1000 мм · печать 1:1

Изм.	Кол.уч	Лист	№ док.	Подп.	Дата
Разраб.		Кырлан А.С.			04.11.26
Пров.					
ГИП					
Н. контр.					
Утв.					

ГД-2026-020-АИ

Квартира 68 м², элитный модерн

Общая площадь 68,47* м² · * размеры приняты, не замерены (реестр — л. 5–7, К-1)

Дизайн-проект интерьера

Стадия	Лист	Листов
РП	36	105

Аксонометрическая схема В1 (холодное водоснабжение)

М 1:50


Кырлан Александр Сергеевич

выпуск 04.11.2026 № 8be4ef4c81 · стр. 41 из 117

Аксонометрическая схема Т3 (горячее водоснабжение)

аксонометрия · диаметры, уклоны, отметки, стояки и приборы · трассы принципиальные

Схема Т3 (М 1:50; по вертикали и горизонтали один масштаб, глубина — ×0,5 под 45°)

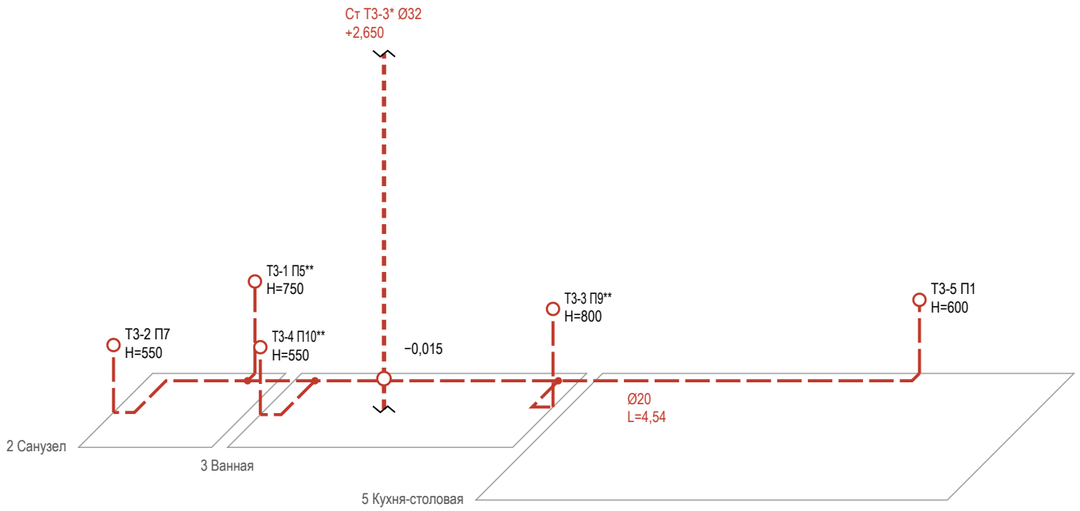

ПРЕДВАРИТЕЛЬНО · не для производства работ · открыто пунктов: 25 (реестр — л. 5–7)

Условные обозначения

- Т3 — горячее водоснабжение, подача (ГВС), PP-R Ø20
- вывод Т3 (код — в ведомости привязок)
- стояк «Ст К1-N / Ст В1-N» (ГОСТ 21.601), Ø мм
- стояк в плане (на отметке пола); вертикаль — стояк по высоте, разрыв — перекрытие
- тройник (ответвление к прибору)
- кран шаровой
- * стояк Т3 не на обмере — принят в шахте рядом со Ст В1, сверить

Допущения и предложения на листе

Основа листа: планировка по обводу плана заказчика, не замерена (К-1); высота до плиты 2650 мм от чистого пола — решение автора (ИЗ-1); отметки плана потолков сдвинуты на -95 мм (+2.745 плана = низ плиты), не замерено (К-2); толщины стен приняты: наружные 260 мм, перегородки 130 мм (К-1); положение стен и проёмов — по брифу без обмера и плана БТИ (К-1); разрешённая мощность 10 кВт принята, ТУ не переданы (К-6); вентканалы приняты, в брифе не заданы (К-5); тип дома, перекрытие и несущие стены не известны — документов нет (К-3); плита электрическая — принята, в брифе не указано (К-6); система заземления TN-C-S принята, ТУ не переданы (К-6); число жильцов 2 принято, в брифе не указано (К-9); подрайон климата не задан — принят не северный (жилые от 2,5 м) (К-26).

Знак «*» — принято, не замерено и не подтверждено (замерить на объекте): К-4: Ст Т3-3, Ст К1-1, Ст В1-2 — положение стояка снято с обвода плана, не замерено.

Знак «**» — предложение проектировщика, заказчиком не утверждено (согласовать с заказчиком): П5 — гигиенический душ у унитаза — предложение по умолчанию (ревизия «квартира под ключ»), заказчик может снять; закладные выводы ставятся до плитки; ИЗ-3, К-7: П10 — раковина у левой стены: светильники 14 плана — у зеркала над ней; отвод К1 к стояку в углу короткий; ИЗ-3, К-28: П9 — ванна 1700 × 750 у правой стены на всю глубину помещения (1700 мм по плану) — стояк в левом углу свободен.

См. лист открытых вопросов (лист 5, записи К-1, К-3–К-7, К-9; лист 6, запись К-26; лист 7, записи ИЗ-3, К-28).

Примечания

1. Схема Т3 построена по тем же трассам, что план разводки: положение в плане сохранено, глубина — в масштабе ×0,5. Трассы принципиальные; фактическое положение фиксируется исполнительной схемой до закрытия.
2. Высоты Н — от чистого пола помещения, мм. Прокладка магистрали Т3 по данным: коллекторная разводка, в стяжке пола, в стяжке пола, выше плиты перекрытия; отметка трасс — по пирогу пола.
3. Узел ввода Т3 (кран, фильтр, счётчик, обратный клапан, кран) — на схеме разводки; состав узла ввода — по согласованию. Кран шаровой — на первом участке от стояка.
4. Циркуляция ГВС в данных не задана — циркуляционного трубопровода на схеме нет (запись реестра К-29).
5. Ст Т3-3* на обмере не показаны: положение принято (исполнитель по плану заказчика), не замерено (К-4); положение сверить на объекте до разводки.
6. Трубы испытать давлением до закрытия (акт скрытых работ, опрессовка по СП 73.13330.2016).
7. Диаметры, высоты выводов и места кранов — по паспортам выбранных приборов и расчёту проектной организации.
8. Расчёт систем, диаметры магистралей и подбор оборудования выполняет проектная организация.

1000 мм · печать 1:1

Изм.	Кол.уч	Лист	№ док.	Подп.	Дата
Разраб.		Кырлан А.С.			04.11.26
Пров.					
ГИП					
Н. контр.					
Утв.					

ГД-2026-020-АИ

Квартира 68 м², элитный модерн

Общая площадь 68,47* м² · * размеры приняты, не замерены (реестр — л. 5–7, К-1)

Дизайн-проект интерьера

Стадия	Лист	Листов
РП	37	105

Аксонометрическая схема Т3 (горячее водоснабжение)

М 1:50

Кырлан Александр Сергеевич


выпуск 04.11.2026 № 8be4ef4c81 · стр. 42 из 117

Аксонометрическая схема К1 (канализация)

аксонометрия · диаметры, уклоны, отметки, стояки и приборы · трассы принципиальные

Схема К1 (М 1:50; по вертикали и горизонтали один масштаб, глубина — ×0,5 под 45°)

ПРЕДВАРИТЕЛЬНО · не для производства работ · открыто пунктов: 25 (реестр — л. 5–7)

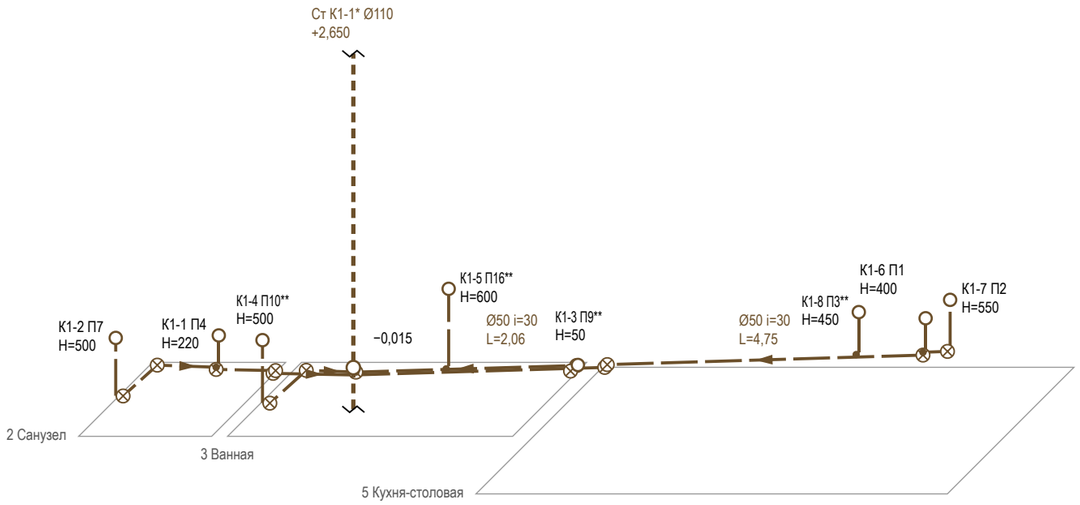

Условные обозначения

- К1 — канализация бытовая
- вывод К1 (код — в ведомости привязок)
- стояк «Ст К1-N / Ст В1-N» (ГОСТ 21.601), Ø мм
- стояк в плане (на отметке пола); вертикаль — стояк по высоте, разрыв — перекрытие
- направление уклона К1 / пола: Ø, мм на 1 м
- ревизия (прочистка) К1 — доступ сохранить
- тройник (ответвление к прибору)
- * стояк Т3 не на обмере — принят в шахте рядом со Ст В1, сверить

Допущения и предложения на листе

Основа листа: планировка по обводу плана заказчика, не замерена (К-1); высота до плиты 2650 мм от чистого пола — решение автора (ИЗ-1); отметки плана потолков сдвинуты на -95 мм (+2.745 плана = низ плиты), не замерено (К-2); толщины стен приняты: наружные 260 мм, перегородки 130 мм (К-1); положение стен и проёмов — по брифу без обмера и плана БТИ (К-1); разрешённая мощность 10 кВт принята, ТУ не переданы (К-6); вентканалы приняты, в брифе не заданы (К-5); тип дома, перекрытие и несущие стены не известны — документов нет (К-3); плита электрическая — принята, в брифе не указано (К-6); система заземления TN-C-S принята, ТУ не переданы (К-6); число жильцов 2 принято, в брифе не указано (К-9); подрайон климата не задан — принят не северный (жилые от 2,5 м) (К-26).

Знак «*» — принято, не замерено и не подтверждено (замерить на объекте): К-4: Ст К1-1, Ст В1-2, Ст Т3-3 — положение стояка снято с обвода плана, не замерено.

Знак «**» — предложение проектировщика, заказчиком не утверждено (согласовать с заказчиком): П3 — питьевая вода без бытового фильтра в доме не гарантирована; фильтр под мойкой — предложение по умолчанию, заказчик может снять (с дренажом отдельной врезкой); ИЗ-3, К-7: П10 — раковина у левой стены: светильники 14 плана — у зеркала над ней; отвод К1 к стояку в углу короткий; П16 — место стиральной машины — в ванной у верхней стены, правее короба стояка; подход 1100 мм перед дверцей, выводы ХВС и К1 Ø40 за машиной; ИЗ-3, К-28: П9 — ванна 1700 × 750 у правой стены на всю глубину помещения (1700 мм по плану) — стояк в левом углу свободен.

См. лист открытых вопросов (лист 5, записи К-1, К-3–К-7, К-9; лист 6, запись К-26; лист 7, записи ИЗ-3, К-28).

Примечания

1. Схема К1 построена по тем же трассам, что план разводки: положение в плане сохранено, глубина — в масштабе ×0,5. Трассы принципиальные; фактическое положение фиксируется исполнительной схемой до закрытия.
2. Отметки — от плиты перекрытия: низ трубы у врезки в стояк — отметка из данных выпуска, к прибору труба поднимается на уклон i, мм/м (уклон не менее 1/d и не более 150 мм/м, СП 30.13330.2020, п. 19.1); чистый пол — выше плиты на стяжку (высота пирога пола). Высота выпуска прибора H — от чистого пола.
3. Ревизия — на повороте и в начале участка; стояк К1 в коробе с люком — звукоизоляция стояка в коробе; поворот — двумя отводами 45°.
4. Ст К1-1* на обмере не показаны: положение принято (исполнитель по плану заказчика), не замерено (К-4); положение сверить на объекте до разводки.
5. Трубы испытать давлением до закрытия (акт скрытых работ, опрессовка по СП 73.13330.2016).
6. Диаметры, высоты выводов и места кранов — по паспортам выбранных приборов и расчёту проектной организации.
7. Расчёт систем, диаметры магистралей и подбор оборудования выполняет проектная организация.

1000 мм · печать 1:1

Изм.	Кол.уч	Лист	№ док.	Подп.	Дата
Разраб.		Кырлан А.С.			04.11.26
Пров.					
ГИП					
Н. контр.					
Утв.					

ГД-2026-020-АИ

Квартира 68 м², элитный модерн

Общая площадь 68,47* м² · * размеры приняты, не замерены (реестр — л. 5–7, К-1)

Дизайн-проект интерьера

Стадия	Лист	Листов
РП	38	105

Аксонометрическая схема К1 (канализация)

М 1:50

Кырлан Александр Сергеевич


выпуск 04.11.2026 № 8be4ef4c81 · стр. 43 из 117

Развёртки мокрых зон: выводы ВК. Санузел


ПРЕДВАРИТЕЛЬНО · не для производства работ · открыто пунктов: 25 (реестр — л. 5–7)

пом. 2 · выводы В1, Т3, К1 на стенах · высоты от чистого пола, привязки от чистовых углов, мм

Стена А (М 1:20)

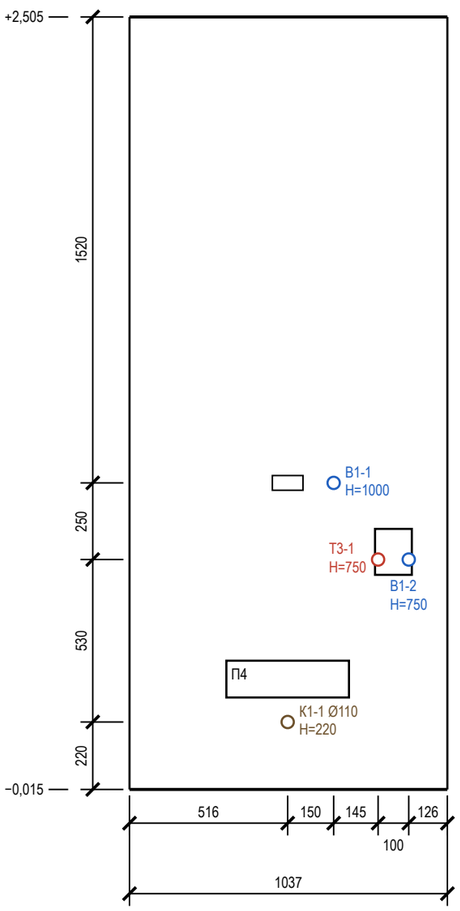

Стена Г (М 1:20)

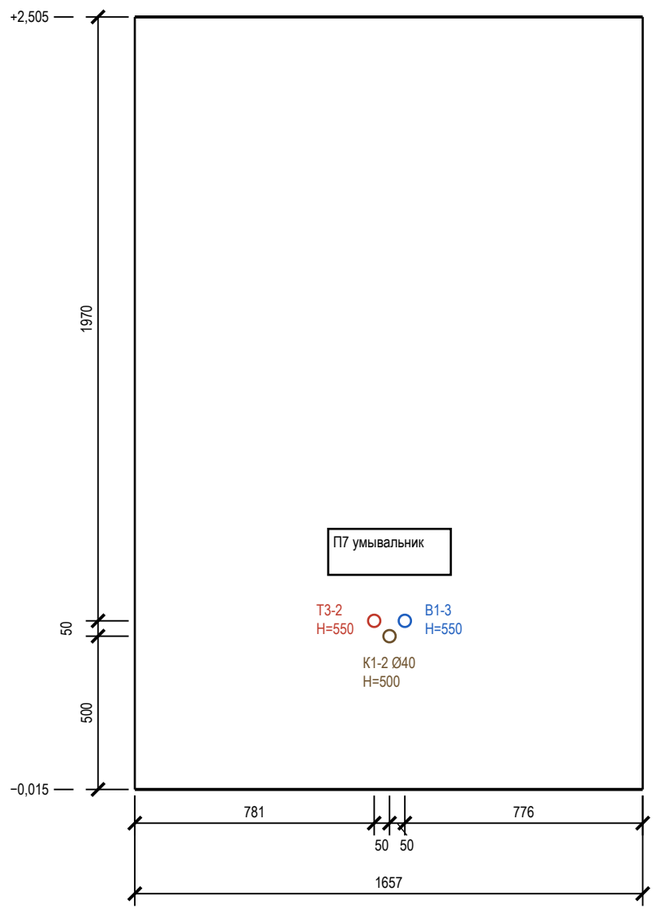

Допущения и предложения на листе

Основа листа: планировка по обводу плана заказчика, не замерена (К-1); высота до плиты 2650 мм от чистого пола — решение автора (ИЗ-1); отметки плана потолков сдвинуты на -95 мм (+2.745 плана = низ плиты), не замерено (К-2); толщины стен приняты: наружные 260 мм, перегородки 130 мм (К-1); положение стен и проёмов — по брифу без обмера и плана БТИ (К-1); разрешённая мощность 10 кВт принята, ТУ не переданы (К-6); вентканалы приняты, в брифе не заданы (К-5); тип дома, перекрытие и несущие стены не известны — документов нет (К-3); плита электрическая — принята, в брифе не указано (К-6); система заземления TN-C-S принята, ТУ не переданы (К-6); число жильцов 2 принято, в брифе не указано (К-9); подрайон климата не задан — принят не северный (жилые от 2,5 м) (К-26).

Знак «**» — предложение проектировщика, заказчиком не утверждено (согласовать с заказчиком): П5 — гигиенический душ у унитаза — предложение по умолчанию (ревизия «квартира под ключ»), заказчик может снять; закладные выводы ставятся до плитки.

Открытые вопросы и конфликты по листу: К-29.

См. лист открытых вопросов (лист 5, записи К-1, К-3, К-5, К-6, К-9; лист 6, запись К-26; лист 7, запись К-29).

Ведомость привязок выводов (от чистого пола и угла)

Код	Прибор	Ø	H, мм	Привязка, мм
В1-1	П4 унитаз подвесной	½"	1000	ст. А: 666 от лев. угла
К1-1	П4 унитаз подвесной	Ø110	220	ст. А: 516 от лев. угла
В1-2	П5** гигиенический душ	½"	750	ст. А: 911 от лев. угла
Т3-1	П5** гигиенический душ	½"	750	ст. А: 811 от лев. угла

Ведомость привязок (продолжение)

Код	Прибор	Ø	H, мм	Привязка, мм
В1-3	П7 умывальник	½"	550	ст. Г: 881 от лев. угла
Т3-2	П7 умывальник	½"	550	ст. Г: 781 от лев. угла
К1-2	П7 умывальник	Ø40	500	ст. Г: 831 от лев. угла

Условные обозначения

- вывод В1 (код — в ведомости привязок)
- вывод Т3 (код — в ведомости привязок)
- вывод К1 (код — в ведомости привязок)
- сантехприбор по расстановке (габарит модели)
- дверной проём; окно — сплошной контур
- кнопка смыва инсталляции (H — по данным прибора)

Примечания

1. Габариты и высоты приборов, межосевые смесителей и места кранов — по паспортам выбранных приборов, сверяются до разметки стен.
2. Высоты H — от чистого пола помещения, мм; отметка чистого пола и потолка — у левого края вида (от ±0,000 объекта). Привязки — от левого чистового угла вида (облицовка стен вычтена), как на развёртках стен.
3. Кнопка смыва П4 — H=1000 (по данным прибора).
4. Ревизионные люки (арматура и ревизии у П4, П5** 300×400, стена А у П4, предложение): привязка к углу — по раскладке плитки, подтверждается обмером.
5. Ревизионные люки к арматуре и ревизиям в данных не заданы: место и размер не определены (записи реестра нет).
6. Расчёт систем водоснабжения и канализации и подбор оборудования выполняет проектная организация; лист задаёт места и высоты выводов.

1000 мм · печать 1:1

Изм.	Кол.уч	Лист	№ док.	Подп.	Дата
Разраб.		Кырлан А.С.			04.11.26
Пров.					
ГИП					
Н. контр.					
Утв.					

ГД-2026-020-АИ

Квартира 68 м², элитный модерн

Общая площадь 68,47* м² · * размеры приняты, не замерены (реестр — л. 5–7, К-1)

Дизайн-проект интерьера

Стадия	Лист	Листов
РП	39	105

Развёртки мокрых зон: выводы ВК. Санузел

М 1:20

Кырлан Александр Сергеевич


выпуск 04.11.2026 № 8be4ef4c81 · стр. 44 из 117

Развёртки мокрых зон: выводы ВК. Ванная (лист 1 из 2)


пом. 3 · выводы В1, Т3, К1 на стенах · высоты от чистого пола, привязки от чистовых углов, мм

ПРЕДВАРИТЕЛЬНО · не для производства работ · открыто пунктов: 25 (реестр — л. 5–7)

Стена А (М 1:20)

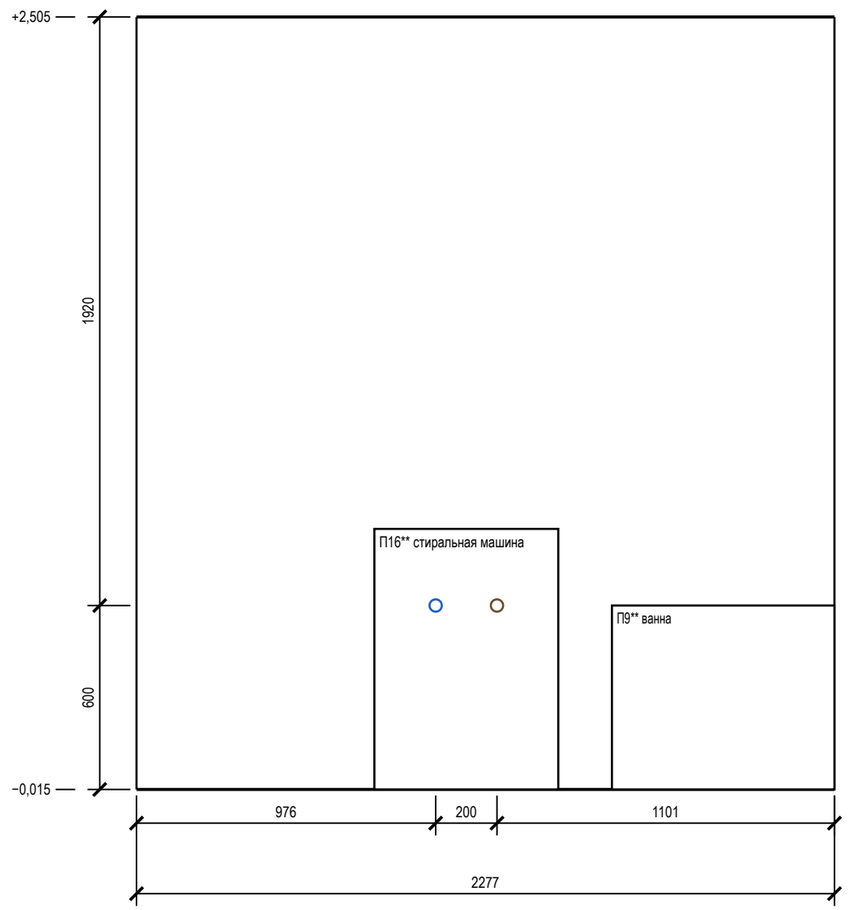

Стена Б (М 1:20)

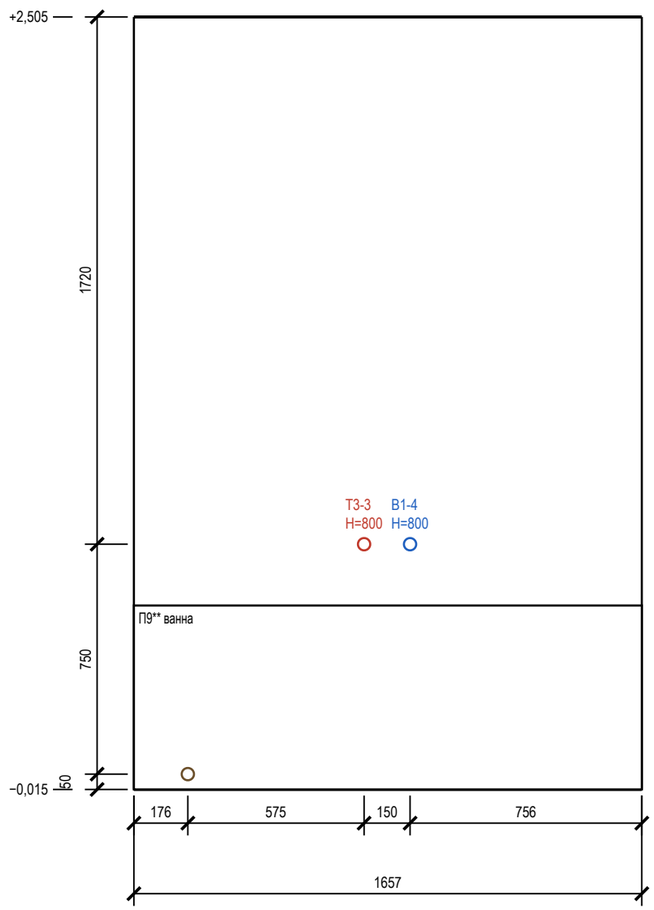

Допущения и предложения на листе

Основа листа: планировка по обводу плана заказчика, не замерена (К-1); высота до плиты 2650 мм от чистого пола — решение автора (ИЗ-1); отметки плана потолков сдвинуты на -95 мм (+2.745 плана = низ плиты), не замерено (К-2); толщины стен приняты: наружные 260 мм, перегородки 130 мм (К-1); положение стен и проёмов — по брифу без обмера и плана БТИ (К-1); разрешённая мощность 10 кВт принята, ТУ не переданы (К-6); вентканалы приняты, в брифе не заданы (К-5); тип дома, перекрытие и несущие стены не известны — документов нет (К-3); плита электрическая — принята, в брифе не указано (К-6); система заземления TN-C-S принята, ТУ не переданы (К-6); число жильцов 2 принято, в брифе не указано (К-9); подрайон климата не задан — принят не северный (жилые от 2,5 м) (К-26).

Знак «*» — принято, не замерено и не подтверждено (замерить на объекте): К-4: Ст К1-1, Ст В1-2, Ст Т3-3 — положение стояка снято с обвода плана, не замерено.

Знак «**» — предложение проектировщика, заказчиком не утверждено (согласовать с заказчиком): ИЗ-3, К-7: П16 — место стиральной машины — в ванной у верхней стены, правее короба стояка; подход 1100 мм перед дверцей, выводы ХВС и К1 Ø40 за машиной; ИЗ-3, К-28: П9 — ванна 1700 × 750 у правой стены на всю глубину помещения (1700 мм по плану) — стояк в левом углу свободен.

Открытые вопросы и конфликты по листу: К-29.

См. лист открытых вопросов (лист 5, записи К-1, К-3–К-7, К-9; лист 6, запись К-26; лист 7, записи ИЗ-3, К-28, К-29).

Ведомость привязок выводов (от чистого пола и угла)

Код	Прибор	Ø	H, мм	Привязка, мм
В1-6	П16** стиральная машина	½"	600	ст. А: 976 от лев. угла
К1-5	П16** стиральная машина	Ø40	600	ст. А: 1176 от лев. угла
В1-4	П9** ванна	½"	800	ст. Б: 901 от лев. угла

Ведомость привязок (продолжение)

Код	Прибор	Ø	H, мм	Привязка, мм
Т3-3	П9** ванна	½"	800	ст. Б: 751 от лев. угла
К1-3	П9** ванна	Ø50	50	ст. Б: 176 от лев. угла

Условные обозначения

- вывод В1 (код — в ведомости привязок)
- вывод Т3 (код — в ведомости привязок)
- вывод К1 (код — в ведомости привязок)
- сантехприбор по расстановке (габарит модели)
- дверной проём; окно — сплошной контур

Примечания

1. Габариты и высоты приборов, межосевые смесителей и места кранов — по паспортам выбранных приборов, сверяются до разметки стен.
2. Высоты Н — от чистого пола помещения, мм; отметка чистого пола и потолка — у левого края вида (от ±0,000 объекта). Привязки — от левого чистового угла вида (облицовка стен вычтена), как на развёртках стен.
3. Стояки в помещении: Ст К1-1* Ø110, Ст В1-2* Ø32, Ст Т3-3* Ø32 — положение на плане выводов; выводы подключаются к ним по схеме разводки.
4. Ревизионные люки (П9** 400×300, стена Б, предложение; узел ввода воды (электрокраны ЭК-1, ЭК-2, счётчики, коллектор) 400×600, стена Б у П9**, предложение): привязка к углу — по раскладке плитки, подтверждается обмером.
5. Ревизионные люки к арматуре и ревизиям в данных не заданы: место и размер не определены (записи реестра нет).
6. Часть подписей выводов не уместилась у знака: коды и высоты — в ведомости привязок.
7. Помещение «Ванная» — 2 листа: стены 1) А, Б; 2) В, Г.
8. Расчёт систем водоснабжения и канализации и подбор оборудования выполняет проектная организация; лист задаёт места и высоты выводов.

1000 мм · печать 1:1

Изм.	Кол.уч	Лист	№ док.	Подп.	Дата
Разраб.		Кырлан А.С.			04.11.26
Пров.					
ГИП					
Н. контр.					
Утв.					

ГД-2026-020-АИ

Квартира 68 м², элитный модерн

Общая площадь 68,47* м² · * размеры приняты, не замерены (реестр — л. 5–7, К-1)

Дизайн-проект интерьера

Стадия	Лист	Листов
РП	40	105

Развёртки мокрых зон: выводы ВК. Ванная
(лист 1 из 2)
М 1:20

Кырлан Александр Сергеевич


выпуск 04.11.2026 № 8be4ef4c81 · стр. 45 из 117

Развёртки мокрых зон: выводы ВК. Ванная (лист 2 из 2)


пом. 3 · выводы В1, Т3, К1 на стенах · высоты от чистого пола, привязки от чистовых углов, мм

ПРЕДВАРИТЕЛЬНО · не для производства работ · открыто пунктов: 25 (реестр — л. 5–7)

Стена В (М 1:20)

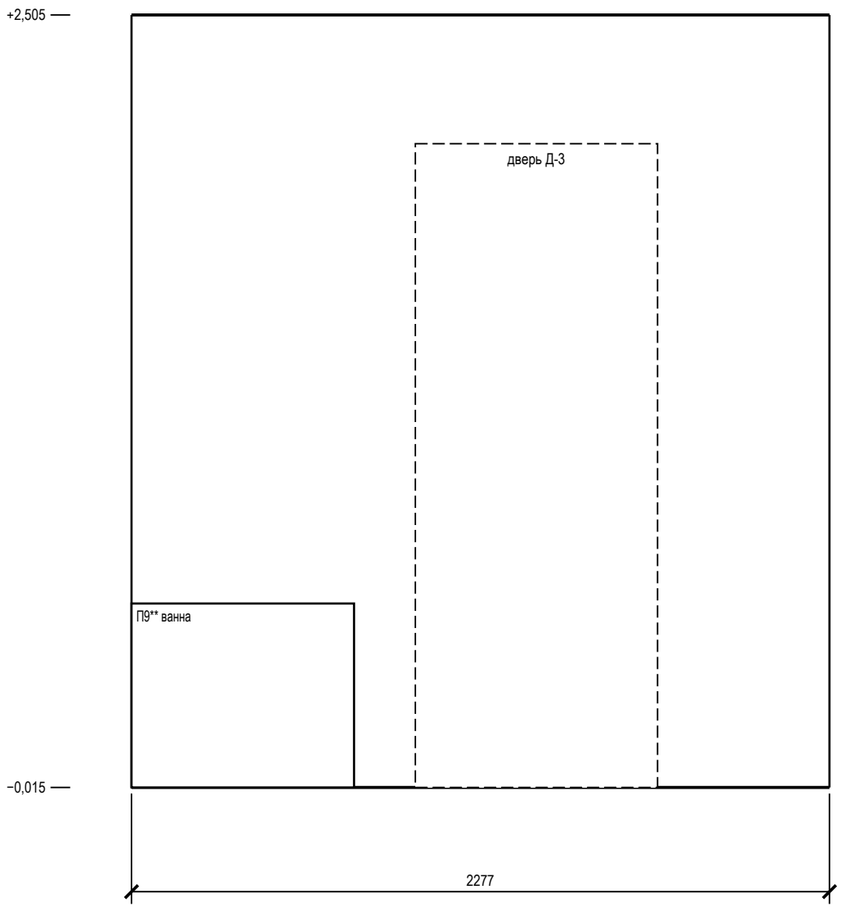

Стена Г (М 1:20)

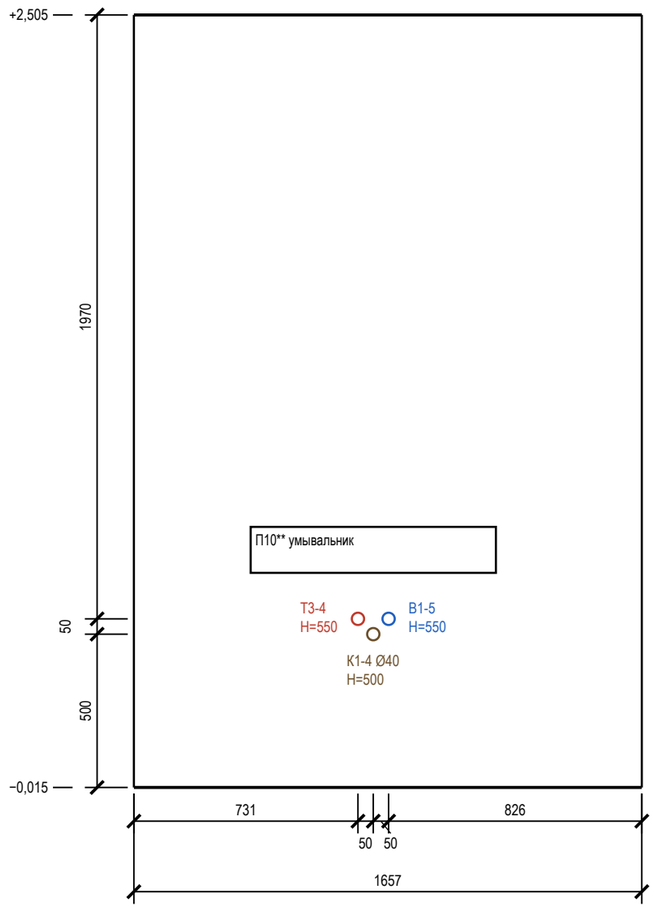

Допущения и предложения на листе

Основа листа: планировка по обводу плана заказчика, не замерена (К-1); высота до плиты 2650 мм от чистого пола — решение автора (ИЗ-1); отметки плана потолков сдвинуты на -95 мм (+2.745 плана = низ плиты), не замерено (К-2); толщины стен приняты: наружные 260 мм, перегородки 130 мм (К-1); положение стен и проёмов — по брифу без обмера и плана БТИ (К-1); разрешённая мощность 10 кВт принята, ТУ не переданы (К-6); вентканалы приняты, в брифе не заданы (К-5); тип дома, перекрытие и несущие стены не известны — документов нет (К-3); плита электрическая — принята, в брифе не указано (К-6); система заземления TN-C-S принята, ТУ не переданы (К-6); число жильцов 2 принято, в брифе не указано (К-9); подрайон климата не задан — принят не северный (жилые от 2,5 м) (К-26).

Знак «*» — принято, не замерено и не подтверждено (замерить на объекте): К-1: дверь пом. 3 (стена В) — проём принят по обводу плана заказчика, без обмера: положение и ширина сняты с плана, не замерены; К-4: Ст К1-1, Ст В1-2, Ст Т3-3 — положение стояка снято с обвода плана, не замерено.

Знак «**» — предложение проектировщика, заказчиком не утверждено (согласовать с заказчиком): ИЗ-3, К-7: П10 — раковина у левой стены: светильники 14 плана — у зеркала над ней; отвод К1 к стояку в углу короткий; ИЗ-3, К-28: П9 — ванна 1700 × 750 у правой стены на всю глубину помещения (1700 мм по плану) — стояк в левом углу свободен.

Открытые вопросы и конфликты по листу: К-29.

См. лист открытых вопросов (лист 5, записи К-1, К-3–К-7, К-9; лист 6, запись К-26; лист 7, записи ИЗ-3, К-28, К-29).

Ведомость привязок выводов (от чистого пола и угла)

Код	Прибор	Ø	H, мм	Привязка, мм
В1-5	П10** умывальник	½"	550	ст. Г: 831 от лев. угла
Т3-4	П10** умывальник	½"	550	ст. Г: 731 от лев. угла
К1-4	П10** умывальник	Ø40	500	ст. Г: 781 от лев. угла

Условные обозначения

- вывод В1 (код — в ведомости привязок)
- вывод Т3 (код — в ведомости привязок)
- вывод К1 (код — в ведомости привязок)
- сантехприбор по расстановке (габарит модели)
- дверной проём; окно — сплошной контур

Примечания

1. Габариты и высоты приборов, межосевые смесителей и места кранов — по паспортам выбранных приборов, сверяются до разметки стен.
2. Высоты H — от чистого пола помещения, мм; отметка чистого пола и потолка — у левого края вида (от ±0,000 объекта). Привязки — от левого чистового угла вида (облицовка стен вычтена), как на развёртках стен.
3. Стояки в помещении: Ст К1-1* Ø110, Ст В1-2* Ø32, Ст Т3-3* Ø32 — положение на плане выводов; выводы подключаются к ним по схеме разводки.
4. Ревизионные люки (П9** 400×300, стена Б, предложение; узел ввода воды (электрокраны ЭК-1, ЭК-2, счётчики, коллектор) 400×600, стена Б у П9**, предложение): привязка к углу — по раскладке плитки, подтверждается обмером.
5. Ревизионные люки к арматуре и ревизиям в данных не заданы: место и размер не определены (записи реестра нет).
6. Помещение «Ванная» — 2 листа: стены 1) А, Б; 2) В, Г.
7. Расчёт систем водоснабжения и канализации и подбор оборудования выполняет проектная организация; лист задаёт места и высоты выводов.

1000 мм · печать 1:1

Изм.	Кол.уч	Лист	№ док.	Подп.	Дата
Разраб.		Кырлан А.С.			04.11.26
Пров.					
ГИП					
Н. контр.					
Утв.					

ГД-2026-020-АИ

Квартира 68 м², элитный модерн

Общая площадь 68,47* м² · * размеры приняты, не замерены (реестр — л. 5–7, К-1)

Дизайн-проект интерьера

Стадия	Лист	Листов
РП	41	105

Развёртки мокрых зон: выводы ВК. Ванная
(лист 2 из 2)
М 1:20

Кырлан Александр Сергеевич


выпуск 04.11.2026 № 8be4ef4c81 · стр. 46 из 117

Развёртки мокрых зон: выводы ВК. Кухня-столовая

пом. 5 · выводы В1, Т3, К1 на стенах · высоты от чистого пола, привязки от чистовых углов, мм

ПРЕДВАРИТЕЛЬНО · не для производства работ · открыто пунктов: 25 (реестр — л. 5–7)

Стена А (М 1:20)

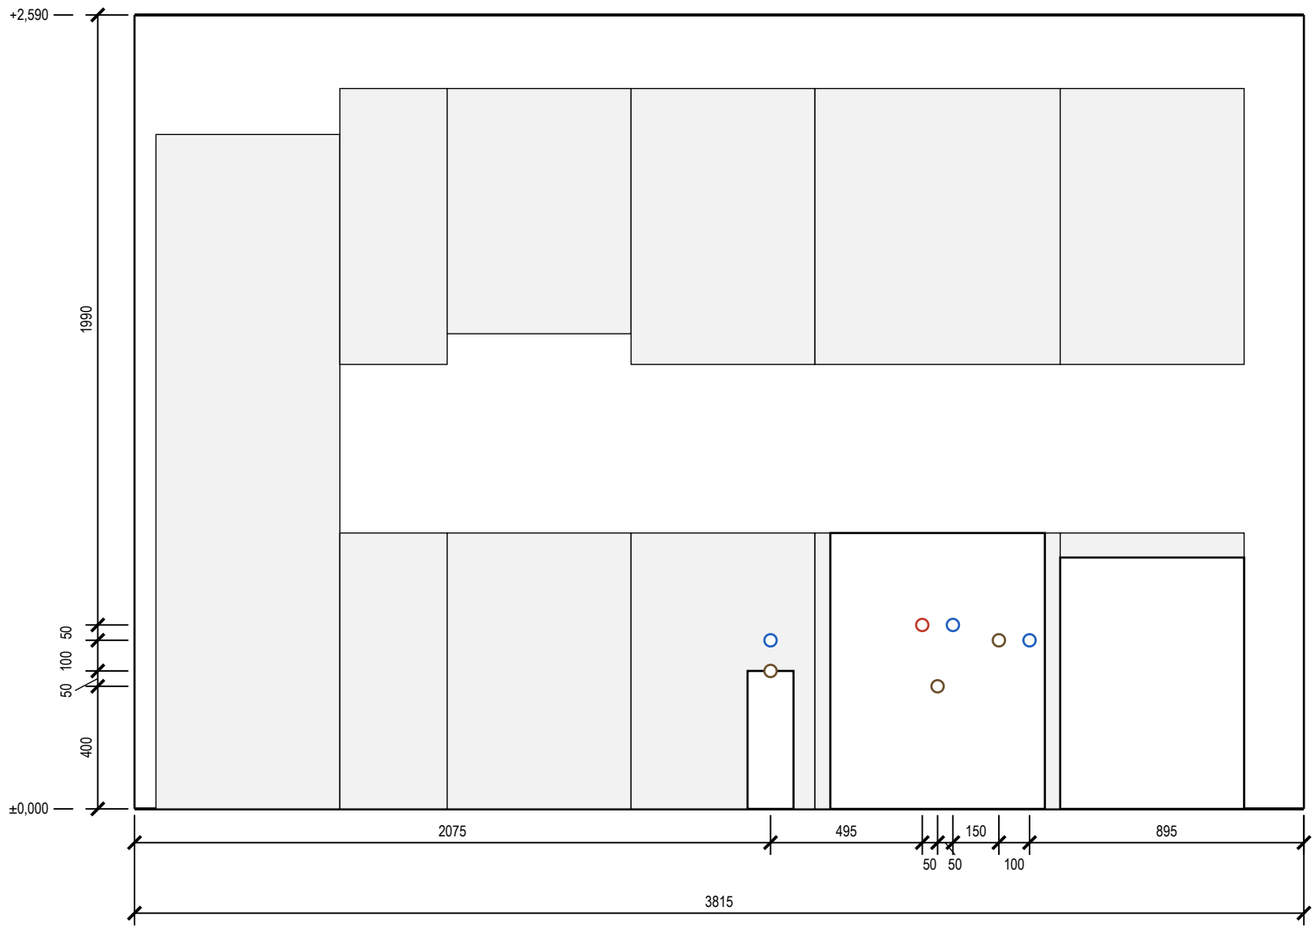

Допущения и предложения на листе

Основа листа: планировка по обводу плана заказчика, не замерена (К-1); высота до плиты 2650 мм от чистого пола — решение автора (ИЗ-1); отметки плана потолков сдвинуты на -95 мм (+2.745 плана = низ плиты), не замерено (К-2); толщины стен приняты: наружные 260 мм, перегородки 130 мм (К-1); положение стен и проёмов — по брифу без обмера и плана БТИ (К-1); разрешённая мощность 10 кВт принята, ТУ не переданы (К-6); вентканалы приняты, в брифе не заданы (К-5); тип дома, перекрытие и несущие стены не известны — документов нет (К-3); плита электрическая — принята, в брифе не указано (К-6); система заземления TN-C-S принята, ТУ не переданы (К-6); число жильцов 2 принято, в брифе не указано (К-9); подрайон климата не задан — принят не северный (жилые от 2,5 м) (К-26).

Знак «**» — предложение проектировщика, заказчиком не утверждено (согласовать с заказчиком): П3 — питьевая вода без бытового фильтра в доме не гарантирована; фильтр под мойкой — предложение по умолчанию, заказчик может снять (с дренажом отдельной врезкой).

Открытые вопросы и конфликты по листу: К-29.

См. лист открытых вопросов (лист 5, записи К-1, К-3, К-5, К-6, К-9; лист 6, запись К-26; лист 7, запись К-29).

Ведомость привязок выводов (от чистого пола и угла)

Код	Прибор	Ø	Н, мм	Привязка, мм
В1-7	П1 мойка кухонная	½"	600	ст. А: 2670 от лев. угла
Т3-5	П1 мойка кухонная	½"	600	ст. А: 2570 от лев. угла
К1-6	П1 мойка кухонная	Ø50	400	ст. А: 2620 от лев. угла
В1-8	П2 посудомоечная машина	½"	550	ст. А: 2920 от лев. угла

Ведомость привязок (продолжение)

Код	Прибор	Ø	Н, мм	Привязка, мм
К1-7	П2 посудомоечная машина	Ø40	550	ст. А: 2820 от лев. угла
В1-9	П3** фильтр обратного осмоса	½"	550	ст. А: 2075 от лев. угла
К1-8	П3** фильтр обратного осмоса	Ø40	450	ст. А: 2075 от лев. угла

Условные обозначения

- вывод В1 (код — в ведомости привязок)
- вывод Т3 (код — в ведомости привязок)
- вывод К1 (код — в ведомости привязок)
- сантехприбор по расстановке (габарит модели)
- дверной проём; окно — сплошной контур

Примечания

1. Габариты и высоты приборов, межосевые смесителей и места кранов — по паспортам выбранных приборов, сверяются до разметки стен.
2. Высоты Н — от чистого пола помещения, мм; отметка чистого пола и потолка — у левого края вида (от ±0,000 объекта). Привязки — от левого чистового угла вида (облицовка стен вычтена), как на развёртках стен.
3. Ревизионные люки (арматура и ревизии у П1, П2, П3** 300×400, стена А у П1, предложение): привязка к углу — по раскладке плитки, подтверждается обмером.
4. Ревизионные люки к арматуре и ревизиям в данных не заданы: место и размер не определены (записи реестра нет).
5. Мойка, ПММ и фильтр — выводы в шкафу мойки; диаметры и положение сифона и кранов сверить по паспортам приборов и чертежам модуля.
6. Часть подписей выводов не уместилась у знака: коды и высоты — в ведомости привязок.
7. Расчёт систем водоснабжения и канализации и подбор оборудования выполняет проектная организация; лист задаёт места и высоты выводов.

1000 мм · печать 1:1

Изм.	Кол.уч	Лист	№ док.	Подп.	Дата
Разраб.		Кырлан А.С.			04.11.26
Пров.					
ГИП					
Н. контр.					
Утв.					

ГД-2026-020-АИ

Квартира 68 м², элитный модерн

Общая площадь 68,47* м² · * размеры приняты, не замерены (реестр — л. 5–7, К-1)

Дизайн-проект интерьера

Стадия	Лист	Листов
РП	42	105

Развёртки мокрых зон: выводы ВК. Кухня-столовая

М 1:20

Кырлан Александр Сергеевич

выпуск 04.11.2026 № 8be4ef4c81 · стр. 47 из 117

Спецификация сантехнического оборудования

Форма 1 ГОСТ 21.110-2013 · ГД-2026-020-АИ-ВК.СО · приборы, арматура, трубопроводы

ПРЕДВАРИТЕЛЬНО · не для производства работ · открыто пунктов: 25 (реестр — л. 5–7)

Поз.	Наименование и техническая характеристика	Тип, марка, обозначение документа	Код продукции	Поставщик	Ед. изм.	Кол.	Масса 1 ед., кг	Примечание
	Санитарные приборы							
1	Ванна встраиваемая акриловая 1700×750 мм, с каркасом, экраном и отверстием слив-перелив	акриловая 1700×750, смеситель настенный		выбор заказчика	шт	1		П9**
2	Унитаз подвесной безободковый, с сиденьем микролифт, крепёж и звукоизолирующая прокладка	инсталляция 1120 + подвесной унитаз		выбор заказчика	шт	1		П4
3	Инсталляция для подвесного унитаза: рама высотой 1120 мм, бачок, клавиша смыва (ось клавиши 1050 мм от чистого пола)	аналог		выбор заказчика	шт	1		П4; короб ГКЛВ
4	Умывальник подвесной 400×280 мм, с отверстием под смеситель и переливом	раковина подвесная 400 × 280, смеситель на раковине аналог по характеристикам		выбор заказчика	шт	1		П7
5	Раковина накладная 800×500 мм, на столешницу тумбы, с переливом	раковина-столешница на подвесной тумбе 800 × 500, смеситель на раковине аналог по характеристикам		выбор заказчика	шт	1		П10**
6	Мойка врезная, нержавеющая сталь 700×480 мм, с переливом	аналог		с кухонной мебелью	шт	1		П1
7	Фильтр обратного осмоса под мойку, с отдельным краном и врезкой дренажа	аналог		выбор заказчика	шт	1		П3**
	Смесители, сифоны и арматура приборов							
8	Смеситель для ванны настенный однорычажный, межосевое 150 мм, с душевым набором (лейка, шланг, держатель)	аналог		выбор заказчика	шт	1		П9**
9	Смеситель для умывальника однорычажный, с донным клапаном	аналог		выбор заказчика	шт	1		П7
10	Смеситель для накладной раковины однорычажный, высокий излив, с донным клапаном	аналог		выбор заказчика	шт	1		П10**
11	Смеситель кухонный однорычажный, высокий излив	аналог		выбор заказчика	шт	1		П1
12	Обвязка ванны слив-перелив Ø40/50 с сифоном	аналог		выбор заказчика	шт	1		П9**
13	Сифон для умывальника бутылочный Ø32/40–50, с гофрой к выпуску	аналог		выбор заказчика	шт	2		П7, П10**
14	Сифон для мойки Ø40/50	аналог		выбор заказчика	шт	1		П1
15	Сифон для посудомоечной машины с обратным клапаном, на выводе слива Ø40	аналог		выбор заказчика	шт	1		П2
16	Сифон для стиральной машины встраиваемый в стену Ø50, с обратным клапаном	аналог		выбор заказчика	шт	1		П16**
17	Кран угловой ½"×½" с гибкой подводкой 40 см (умывальники, мойка)	аналог		выбор заказчика	шт	6		по 2 на прибор
18	Кран шаровой угловой ½"×¾" для подключения стиральной и посудомоечной машины	аналог		выбор заказчика	шт	2		П16**, П2
	Трубопроводы							
19	Труба полипропиленовая PP-R PN20 Ø20×3,4 (В1)	ГОСТ 32415-2013		выбор заказчика	м	17,5	0,17	9,8 + 6,0 + 10 %
20	Труба PP-R, армированная стекловолокном, PN20 Ø20×2,8 (Т3)	ГОСТ 32415-2013		выбор заказчика	м	14	0,15	9,1 + 3,3 + 10 %
21	Труба канализационная ПП Ø40 (К1)	ГОСТ 32414-2013		выбор заказчика	м	6,5		3,0 + 2,6 + 10 %
22	Труба канализационная ПП Ø50 (К1)	ГОСТ 32414-2013		выбор заказчика	м	8		6,8 + 0,5 + 10 %
23	Труба канализационная ПП Ø110 (К1)	ГОСТ 32414-2013		выбор заказчика	м	2		1,3 + 0,2 + 10 %
	Фасонные части и выводы							
24	Отвод канализационный ПП 45° Ø40	ГОСТ 32414-2013		выбор заказчика	шт	10		2 шт. на поворот
25	Отвод канализационный ПП 45° Ø50	ГОСТ 32414-2013		выбор заказчика	шт	12		2 шт. на поворот
26	Отвод канализационный ПП 45° Ø110	ГОСТ 32414-2013		выбор заказчика	шт	6		2 шт. на поворот
27	Тройник канализационный ПП 45° (врезки ветвей)	ГОСТ 32414-2013		выбор заказчика	шт	7		
28	Ревизия канализационная ПП (после поворота трассы)	ГОСТ 32414-2013		выбор заказчика	шт	8		доступ сохранить
29	Фитинги PP-R Ø20: тройники, угольники 90° (ветви и повороты В1, Т3)	ГОСТ 32415-2013		выбор заказчика	шт	23		
30	Водорозетка PP-R Ø20×½" настенная, с креплением	ГОСТ 32415-2013		выбор заказчика	шт	14		коды — лист выводов
	Узлы ввода, люки, короба							
31	Кран шаровой латунный Ду15 PN16 (отключение ввода)	аналог		выбор заказчика	шт	2		Ст В1-2*, Ст Т3-3*
32	Фильтр сетчатый косой Ду15	аналог		выбор заказчика	шт	2		
33	Счётчик воды крыльчатый Ду15 (ХВ, ГВ), с поверкой	аналог		выбор заказчика	шт	2		пломба УК
34	Клапан обратный Ду15	аналог		выбор заказчика	шт	2		
35	Люк ревизионный нажимной под плитку 300×400 мм	аналог		выбор заказчика	шт	4		к стоякам и арматуре
36	Звукоизоляция стояка К1 в коробе: рулонный звукоизоляционный материал ≥ 10 мм, обмотка стояка на высоту этажа	аналог		выбор заказчика	м	2,7		Ст К1-1*
37	Короб К1 над полом: профиль ПН/ПС, ГКЛВ 12,5 мм под плитку	аналог		выбор заказчика	м	2,3		сечение — лист разводки

Примечания

1. Форма 1 ГОСТ 21.110-2013, ширины граф изменены по п. 4.1. «Аналог» — аналог по характеристикам: модели внести до черновых работ, привязки выводов сверить по паспортам.
2. Бытовая техника не входит (показана арматура подключения), мойка — в комплекте кухни (марка — модуля кухни, как у столяра). Длины труб — трасса листа разводки + подъёмы + 10 %.
3. Стояк К1 в коробе — звукоизоляция стояка в коробе без жёсткого контакта короба с трубой. Стояки со «*» (Ст К1-1*, Ст В1-2*, Ст Т3-3*) приняты положение и число узлов ввода сверить на объекте.
4. Расчёт систем водоснабжения и канализации, диаметры магистралей и подбор оборудования выполняет проектная организация.

Допущения и предложения на листе

Основа листа: планировка по обводу плана заказчика, не замерена (К-1); высота до плиты 2650 мм от чистого пола — решение автора (ИЗ-1); отметки плана потолков сдвинуты на -95 мм (+2.745 плана = низ плиты), не замерено (К-2); толщины стен приняты: наружные 260 мм, перегородки 130 мм (К-1); положение стен и проёмов — по брифу без обмера и плана БТИ (К-1); разрешённая мощность 10 кВт принята, ТУ не переданы (К-6); вентканалы приняты, в брифе не заданы (К-5); тип дома, перекрытие и несущие стены не известны — документов нет (К-3); плита электрическая — принята, в брифе не указано (К-6); система заземления TN-C-S принята, ТУ не переданы (К-6); число жильцов 2 принято, в брифе не указано (К-9); подрайон климата не задан — принят не северный (жилые от 2,5 м) (К-26).

Знак «*» — принято, не замерено и не подтверждено (замерить на объекте): К-4: Ст К1-1, Ст В1-2, Ст Т3-3 — положение стояка снято с обвода плана, не замерено.

Знак «**» — предложение проектировщика, заказчиком не утверждено (согласовать с заказчиком): П3 — питьевая вода без бытового фильтра в доме не гарантирована; фильтр под мойкой — предложение по умолчанию, заказчик может снять (с дренажом отдельной врезкой); ИЗ-3, К-7: П10 — раковина у левой стены: светильники 14 плана — у зеркала над ней; отвод К1 к стояку в углу короткий; П16 — место стиральной машины — в ванной у верхней стены, правее короба стояка; подход 1100 мм перед дверцей, выводы ХВС и К1 Ø40 за машиной; ИЗ-3, К-28: П9 — ванна 1700 × 750 у правой стены на всю глубину помещения (1700 мм по плану) — стояк в левом углу свободен.

См. лист открытых вопросов (лист 5, записи К-1, К-3–К-7, К-9; лист 6, запись К-26; лист 7, записи ИЗ-3, К-28).

Изм.	Кол.уч	Лист	№ док.	Подп.	Дата
Разраб.		Кырлан А.С.			04.11.26
Пров.					
ГИП					
Н. контр.					
Утв.					

ГД-2026-020-АИ

Квартира 68 м², элитный модерн

Общая площадь 68,47* м² · * размеры приняты, не замерены (реестр — л. 5–7, К-1)

Дизайн-проект интерьера

Стадия	Лист	Листов
РП	43	105

Спецификация сантехнического оборудования

М б/м

Кырлан Александр Сергеевич

выпуск 04.11.2026 № 8be4ef4c81 · стр. 48 из 117

Техническое задание на подбор светильников

Параметры для подбора: светильники, ленты и блоки питания, слои света · б/м

Параметры светильников для подбора

Поз.	Марки	Наименование	Установка	Кол.	P, Вт	Σ P, Вт	Ф, лм	Тц, К	Ra	Угол, °	IP	Дим.	Слой	Группа	Пом.
1	Св1**, Св2**, Св3**, Св4**, Св5**, Св6**, Св10**, Св11**, Св12**, Св13**, Св14**, Св15**, Св16**, Св17**, Св19**, Св26**, Св27**, Св28**, Св29**, Св30**, Св31**, Св36**, Св37**, Св38**, Св39**, Св40**, Св41**, Св42**, Св43**	Встраиваемый точечный, встраиваемый LED-светильник, монтажная глубина ≤ 50 мм аналог по характеристикам	в ГКЛ, корпус ≤ 50 мм	29	7	203	600	2700	90	—	20	—	общий	L1, L2, L3, L6, L7, L8, L9	1, 4, 5, 6, 7
2	Св7**	Настенный (бра)	на стене, H=1500	1	5	5	300	2700	90	—	20	—	рабочий	L1	1
3	Св44**, Св46**, Св47**, Св48**, Св49**, Св50**, Св51**	Встраиваемый точечный, встраиваемый LED-светильник IP44, монтажная глубина ≤ 50 мм — аналог по характеристикам	в ГКЛ, корпус ≤ 50 мм	7	7	49	600	2700	90	—	44	—	общий	L11, L13	2, 3
4	Св52**, Св53**, Св54**, Св55**, Св56**, Св57**	Встраиваемый точечный	в ГКЛ, корпус ≤ 50 мм	6	5	30	400	2700	90	24	20	—	акцентный	L2	4
5	Св18	Линейный настенный	под верхними шкафами, H=1400	1	30	30	2400	2700	90	—	20	—	рабочий	L4	5
6	Св58**, Св59**	Подвесной	подвес	2	6	12	400	2700	90	—	20	—	рабочий	L10	7
		Итого		**46 шт**		**329**									

LED-ленты, линейные светильники и блоки питания

Марка	Пом.	L, м	U, В	Вт/м	Σ P, Вт	БП	P БП, Вт	Загр., %	Питание	Доступ к БП
Св18	5	3	—	—	30	у ленты	36	83	встроенный ввод	люк ревизии 300×300 мм

Слои света

общий — равномерный свет помещения, по норме освещённости

рабочий — местный свет задачи: столешница, зеркало, чтение у кровати

акцентный — подсветка потолка, стен и ниш; не входит в поток общего света

Слои света по помещениям

Пом.	Помещение	Слои света — группы включения (марки — в спецификации)	Σ P, Вт
1	Кабинет	общий — L1; рабочий — L1	47
2	Санузел	общий — L11	7
3	Ванная	общий — L13	42
4	Прихожая	общий — L2; акцентный — L2	51
5	Кухня-столовая	общий — L3, L6; рабочий — L4	72
6	Гостиная	общий — L7, L8	42
7	Спальня	общий — L9; рабочий — L10	68

Допущения и предложения на листе

Основа листа: планировка по обводу плана заказчика, не замерена (К-1); высота до плиты 2650 мм от чистого пола — решение автора (ИЗ-1); отметки плана потолков сдвинуты на -95 мм (+2.745 плана = низ плиты), не замерено (К-2); толщины стен приняты: наружные 260 мм, перегородки 130 мм (К-1); положение стен и проёмов — по брифу без обмера и плана БТИ (К-1); разрешённая мощность 10 кВт принята, ТУ не переданы (К-6); вентканалы приняты, в брифе не заданы (К-5); тип дома, перекрытие и несущие стены не известны — документов нет (К-3); плита электрическая — принята, в брифе не указано (К-6); система заземления TN-C-S принята, ТУ не переданы (К-6); число жильцов 2 принято, в брифе не указано (К-9); подрайон климата не задан — принят не северный (жилые от 2,5 м) (К-26).

Знак «**» — предложение проектировщика, заказчиком не утверждено (согласовать с заказчиком): К-20: Св1, Св2, Св3, Св4, Св5, Св6, Св7, Св44, Св46, Св47, Св48, Св49, Св50, Св51, Св10, Св11, Св12, Св13, Св14, Св15, Св16, Св17, Св19, Св26, Св27, Св28, Св29, Св30, Св31, Св36, Св37, Св38, Св39, Св40, Св41, Св42, Св43, Св58, Св59 — место и марка — по исходному плану потолков (±30 мм по рисунку); тип, мощность и цвет света — допущение исполнителя; Св52, Св53, Св54, Св55, Св56, Св57 — место и марка — по исходному плану потолков (±30 мм по рисунку); тип, мощность и цвет света — допущение исполнителя; в нише по плите (ж/б) встроить некуда — накладные.

См. лист открытых вопросов (лист 5, записи К-1, К-3, К-5, К-6, К-9; лист 6, записи К-20, К-26).

Примечания

1. Позиции и марки Св — те же, что на плане освещения (лист 24) и в ведомости светильников (лист 26); группы L — по плану выключателей (лист 25).
2. Модели выбраны не у всех позиций: лист — техническое задание на подбор. Модель по строке таблицы: поток, Тц, Ra, угол, IP и регулировка яркости не хуже указанных, мощность не больше; встраиваемые — под глубину короба (графа «Установка»). IP 20 — сухие помещения. После выбора моделей (артикул, производитель) лист выпускается как «Спецификация светильников».
3. Мощность и поток в таблице — требования к подбору (поток не меньше, мощность не больше указанных); после выбора модели — по её паспорту, Σ P — установленная мощность освещения. Оценка освещённости — на плане освещения; это не светотехнический расчёт.

Изм.	Кол.уч	Лист	№ док.	Подп.	Дата
Разраб.		Кырлан А.С.			04.11.26
Пров.					
ГИП					
Н. контр.					
Утв.					

ГД-2026-020-АИ

Квартира 68 м², элитный модерн

Общая площадь 68,47* м² · * размеры приняты, не замерены (реестр — л. 5–7, К-1)

Дизайн-проект интерьера

Стадия	Лист	Листов
РП	44	105

Техническое задание на подбор светильников

М б/м

Кырлан Александр Сергеевич

выпуск 04.11.2026 № 8be4ef4c81 · стр. 49 из 117

06

Потолки и ГКЛ-конструкции

Кырлан Александр Сергеевич


выпуск 04.11.2026 · 8be4ef4c81 · стр. 50 из 117

План потолков

Уровни и марки потолков, короба с подсветкой, ниши под шторы, люки, вырезы · отметки низа от ±0,000 чистого пола · размеры в мм

ПРЕДВАРИТЕЛЬНО · не для производства работ · открыто пунктов: 25 (реестр — л. 5–7)

Допущения и предложения на листе. Знак «*» принято (замерить): Ст К1-1, Ст В1-2, Ст Т3-3. Знак «**» предложено (согласовать). См. лист открытых вопросов (листы 5–7).

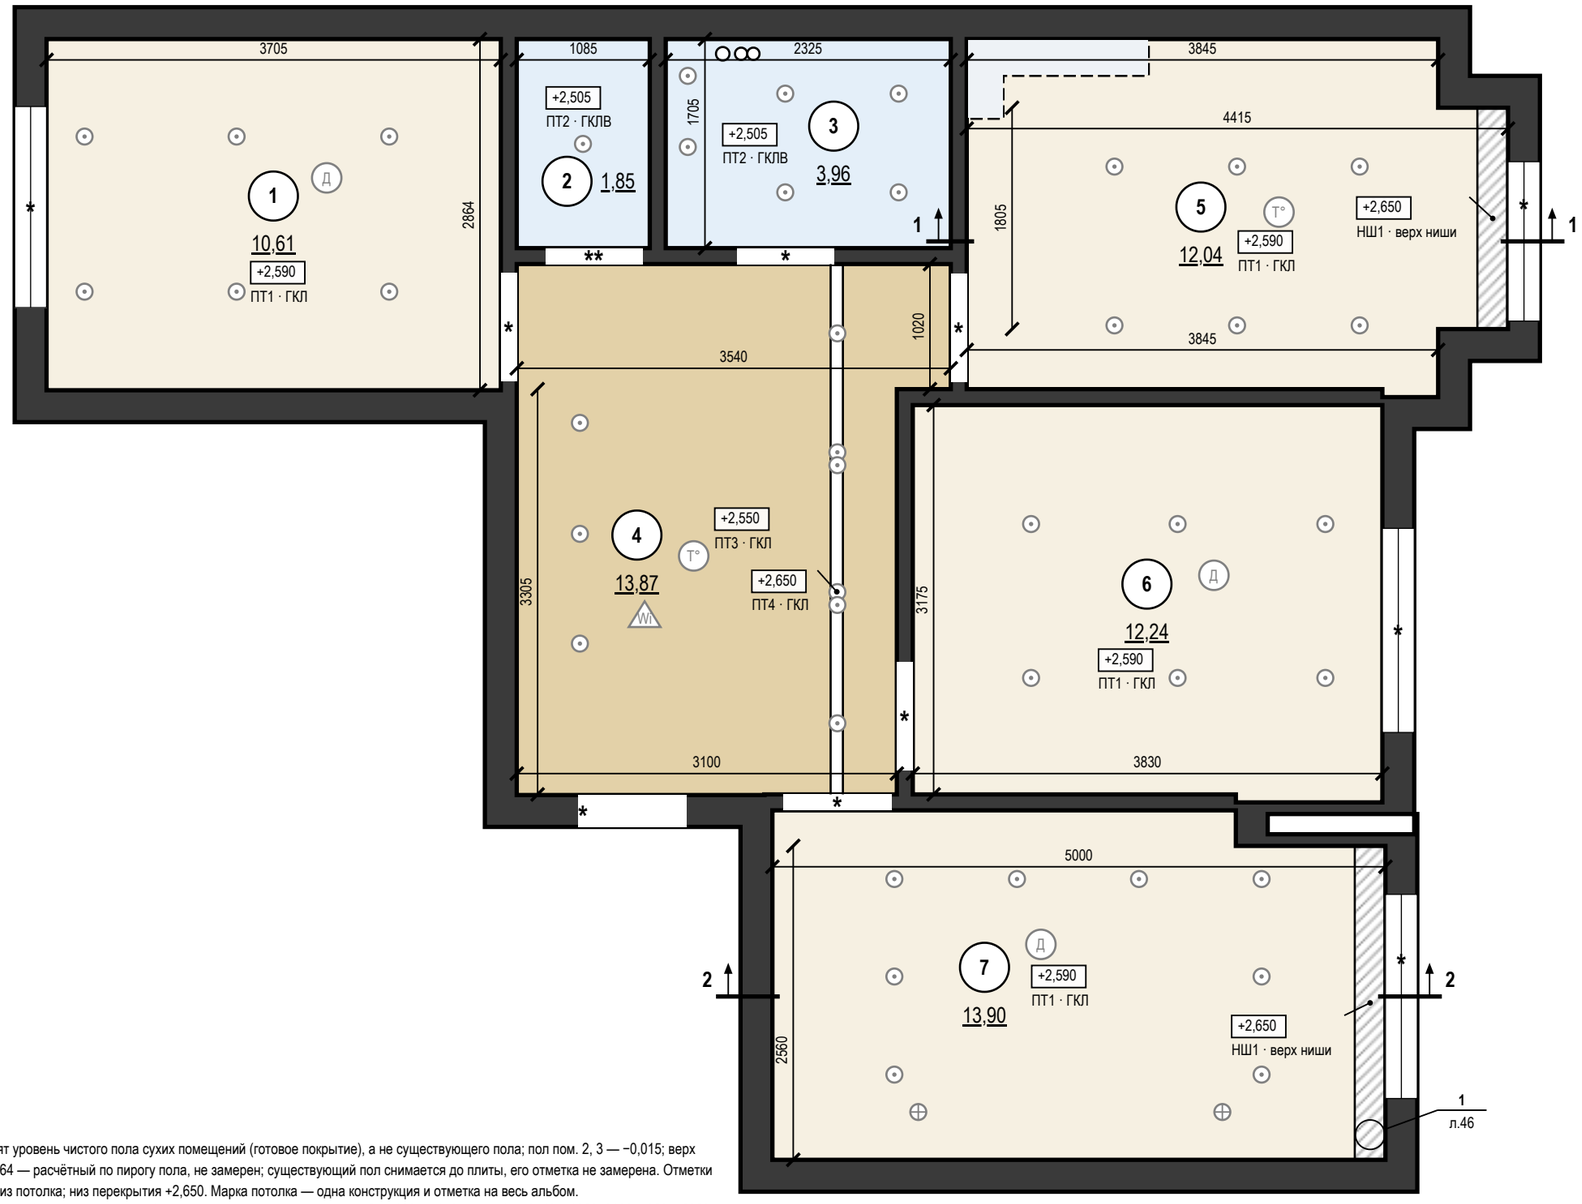

Ведомость потолков

Пом.	Марка	Конструкция	Низ / верх ниши	S, м²	Q
1	ПТ1	ГКЛ П113	+2,590	10,61	Q3
2	ПТ2	ГКЛВ П113	+2,505	1,85	Q3
3	ПТ2	То же	+2,505	3,96	Q3
4	ПТ3	ГКЛ П113	+2,550	13,44	Q3
4	ПТ4	Существующий потолок	+2,650	0,43	
5	ПТ1	ГКЛ П113	+2,590	11,59	Q3
5	НШ1	ниша под шторы 250×60	+2,650	0,45	
6	ПТ1	ГКЛ П113	+2,590	12,24	Q3
7	ПТ1	То же	+2,590	13,26	Q3
7	НШ1	ниша под шторы 250×60	+2,650	0,64	
		Итого		**68,47**	

Условные обозначения

- ПТ1 — ГКЛ по каркасу П113, низ +2,590
- ПТ2 — ГКЛВ по каркасу П113, низ +2,505
- ПТ3 — ГКЛ по каркасу П113, низ +2,550
- ПТ4 — ГКЛ по каркасу, низ +2,650
- НШ1 — ниша под шторы 250×60, верх +2,650
- граница уровней потолка (перепад)
- стояк: К1 — канализация, В1 — ХВС, Т3 — ГВС
- светильник встраиваемый — подложка с плана освещения
- светильник подвесной — подложка с плана освещения
- Д — извещатель дымовой на потолке — подложка
- Т° — извещатель тепловой на потолке — подложка
- Wi — точка доступа Wi-Fi на потолке — подложка
- короб воздуховода вытяжки ГКЛ (трасса — план вентиляции)
- линия разреза у стен помещения, стрелка — направление взгляда
- место узла: номер узла на полке, под полкой — лист
- +2,600 — отметка низа потолка, м (у ниши под шторы — верх ниши); под ней марка потолка
- 1 — номер помещения, площадь м²

Примечания

1. За отметку ±0,000 принят уровень чистого пола сухих помещений (готовое покрытие), а не существующего пола; пол пом. 2, 3 — −0,015; верх плиты перекрытия −0,064 — расчётный по пирогу пола, не замерен; существующий пол снимается до плиты, его отметка не замерена. Отметки в прямоугольниках — низ потолка; низ перекрытия +2,650. Марка потолка — одна конструкция и отметка на весь альбом.
2. Размеры помещений в свету (ширина × длина, мм), не поместившиеся на плане: пом. 2 — 1085 × 1705; пом. 4 — 3540 × 1020, 3100 × 3305, 2020 × 5; пом. 6 — 3830 × 3175, 1195 × 65; пом. 7 — 3780 × 290, 5000 × 2560.
3. Потолки ГКЛ — каркасная система П113: подвесы через 1000 (с запасом: СП 163, табл. 14 — до 1100 при 0,15 кН/м²), несущие профили через 500, основные через 1200 мм; листы — поперёк несущих профилей. В помещениях 2, 3 — ГКЛВ на оцинкованном каркасе.
4. Ниши под шторы 250×60 мм — на всю длину стены с окном; карниз — на закладной до обшивки (узел 1, лист 46).
5. Примыкание к стенам: теневой шов 15 мм, техзазор 3 мм — пом. 1, 4, 5, 6, 7, по стенам, выровненным штукатуркой (узел 1); пом. 2, 3 разделительная лента.
6. Светильники и потолочные устройства — подложка с планов освещения, слаботочных систем и вентиляции (положение — по ним); вырезы и закладные — по ведомости на листе, до обшивки; отверстия не совмещать с профилями, глубина корпуса светильника до 50 мм.
7. Разрезы 1–1, 2–2 — на листе 46; высоты мебели и дверных блоков сверены с низом потолка в разрезах.
8. Узлы по выноскам на плане: узел 1 — лист 46; сечения М 1:10 по помещениям — лист 48.
9. Шпаклевание ГКЛ и условия приёмки — Q3: рассеянный дневной свет, осмотр с 2 м; боковой свет не оценивается.
10. Ведомость вырезов и закладных в потолке — на листе 46; вырезы и закладные — до обшивки.
11. Пом. 5: короб воздуховода кухонной вытяжки ГКЛ 300×130 мм (ширина от стены × высота), низ +2,520, длина 1,53 м — по трассе плана вентиляции, вдоль стен до входа в канал; под плоский воздуховод 200×60 (сечение ≈ Ø125): круглый Ø125 в коробе 200 мм опустил бы кухню ниже 2,5 м — сечение подтверждает раздел ОВ; каркас ПН 28×27 по стене и плите, ПП 60×27, лист ГКЛ 12,5.
12. Сечения потолков М 1:10: пом. 5 — 5.1, 5.2 (лист 48); пом. 7 — 5.1, 5.2 (лист 48).

1000 мм · печать 1:1

Изм.	Кол.уч	Лист	№ док.	Подп.	Дата
Разраб.		Кырлан А.С.			04.11.26
Пров.					
ГИП					
Н. контр.					
Утв.					

ГД-2026-020-АИ

Квартира 68 м², элитный модерн

Общая площадь 68,47* м² · * размеры приняты, не замерены (реестр — л. 5–7, К-1)

Дизайн-проект интерьера

Стадия	Лист	Листов
РП	45	105

План потолков

М 1:50

Кырлан Александр Сергеевич


выпуск 04.11.2026 № 8be4ef4c81 · стр. 51 из 117

Разрезы и узлы потолков

Разрезы по потолкам с отметками уровней · узлы коробов и ниш · ведомость вырезов и закладных · размеры в мм


Разрез 1–1 (М 1:40)

Пом. 5 Кухня-столовая; линия разреза — план потолков, лист 45

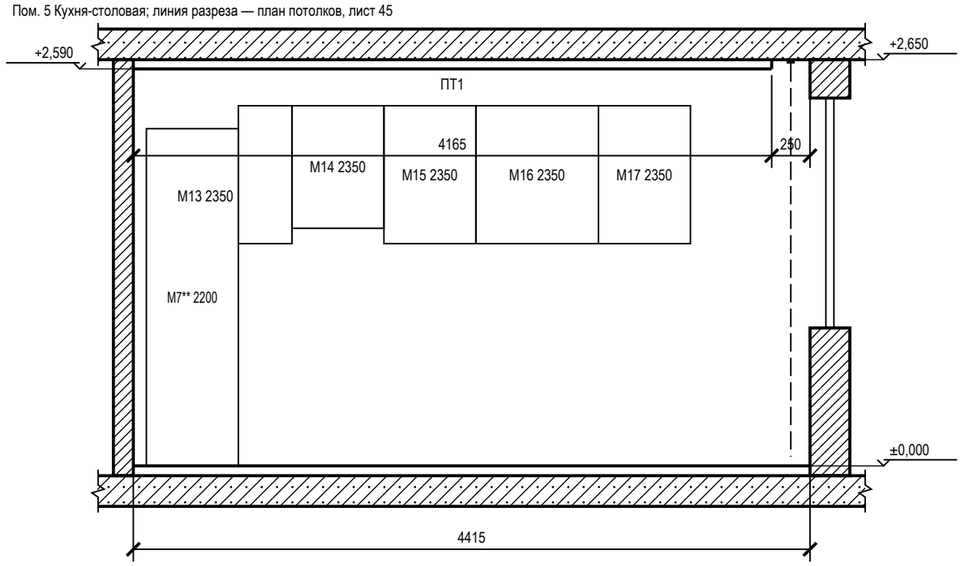


Разрез 2–2 (М 1:40)

Пом. 7 Спальня; линия разреза — план потолков, лист 45

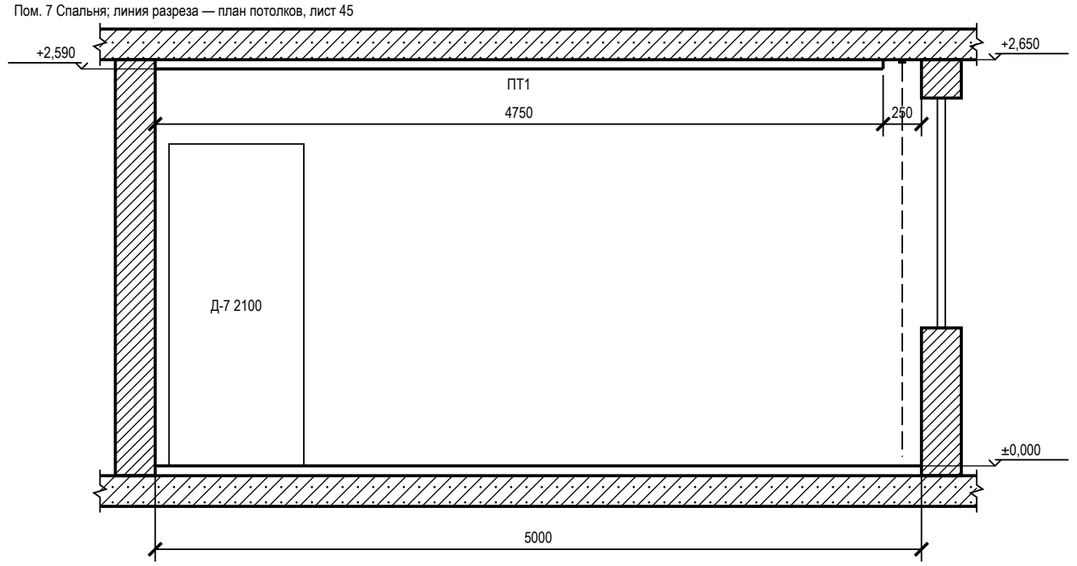

1 Ниша под шторы (М 1:10)

Пом. 5, 7; без подсветки; закладные под карниз — до обшивки

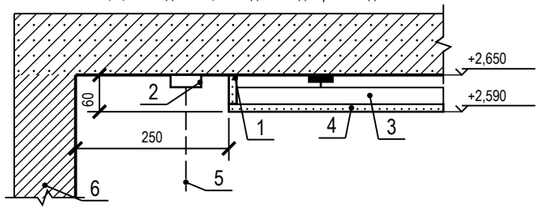

1 — стенка ниши — ГКЛ 12,5
2 — карниз (шина), высота с верхом портьеры 60 мм
3 — ПП 60×27 — каркас короба
4 — низ короба нижнего уровня — ГКЛ 12,5
5 — портьера
6 — стена с окном

Условные обозначения

- плита перекрытия в сечении
- стена в сечении
- потолок ГКЛ в сечении; под линией — марка потолка (план потолков)
- мебель и дверные проёмы за секущей плоскостью; число — марка и верх от чистого пола, мм
- портьера в нише под шторы

Ведомость вырезов и закладных в потолке

Марка	Устройство	Кол.	Пом.
	Светильник встраиваемый (марки — план освещения)	42	1, 2, 3, 4, 5, 6, 7
	Светильник подвесной (марки — план освещения)	2	7
ИП1, ИП4, ИП5	Извещатель дымовой	3	1, 6, 7
ИП2, ИП3	Извещатель тепловой	2	4, 5
АР1**	Точка доступа Wi-Fi, PoE	1	4

Допущения и предложения на листе

Основа листа: планировка по обводу плана заказчика, не замерена (К-1); высота до плиты 2650 мм от чистого пола — решение автора (ИЗ-1); отметки плана потолков сдвинуты на -95 мм (+2.745 плана = низ плиты), не замерено (К-2); толщины стен приняты: наружные 260 мм, перегородки 130 мм (К-1); положение стен и проёмов — по брифу без обмера и плана БТИ (К-1); разрешённая мощность 10 кВт принята, ТУ не переданы (К-6); вентканалы приняты, в брифе не заданы (К-5); тип дома, перекрытие и несущие стены не известны — документов нет (К-3); плита электрическая — принята, в брифе не указано (К-6); система заземления TN-C-S принята, ТУ не переданы (К-6); число жильцов 2 принято, в брифе не указано (К-9); подрайон климата не задан — принят не северный (жилые от 2,5 м) (К-26).

Знак «**» — предложение проектировщика, заказчиком не утверждено (согласовать с заказчиком): АР1 — точка доступа Wi-Fi: число и места; К-7: М7.

См. лист открытых вопросов (лист 5, записи К-1, К-3, К-5–К-7, К-9; лист 6, запись К-26).

Примечания

1. Разрезы — по линиям 1–1, 2–2 на плане потолков (лист 45). Отметки — от ±0,000 чистого пола, м; размеры — мм.
2. Высоты мебели и дверных блоков за секущей плоскостью сверены с низом потолка над ними: верх ниже низа короба и поля.
3. ГКЛ 12,5 мм по каркасу П113. Ниша под шторы — на всю длину стены с окном, карниз на закладной до обшивки (узел 1 — на этом листе).
4. Толщины плит перекрытия и пирога пола показаны условно.
5. Сечения потолков по помещениям М 1:10 (отметки помещения, профили, подвесы, крепёж, изделия) — лист 48.
6. Ведомость вырезов и закладных в потолке — к плану потолков (лист 45): вырезы и закладные — до обшивки, марки светильников — по плану освещения.
7. Ведомость объёмов потолков (лист ГКЛ, профиль, подвесы, лента, блоки питания, люки) — на листе 47.

1000 мм · печать 1:1

Изм.	Кол.уч	Лист	№ док.	Подп.	Дата
Разраб.		Кырлан А.С.			04.11.26
Пров.					
ГИП					
Н. контр.					
Утв.					

ГД-2026-020-АИ

Квартира 68 м², элитный модерн

Общая площадь 68,47* м² · * размеры приняты, не замерены (реестр — л. 5–7, К-1)

Дизайн-проект интерьера

Стадия	Лист	Листов
РП	46	105

Разрезы и узлы потолков

М 1:40; 1:10

Кырлан Александр Сергеевич

выпуск 04.11.2026 № 8be4ef4c81 · стр. 52 из 117

Разрезы и узлы потолков (продолжение)

Ведомость объёмов · размеры в мм

Ведомость объёмов потолков

Позиция	Ед.	Кол.	Пом.
Лист ГКЛ 12,5	м²	62,91	1, 4, 5, 6, 7
Лист ГКЛВ 12,5	м²	5,81	2, 3
Борта и карнизы (входят в площади листов выше)	м²	0,69	4, 5, 7
Профиль ПП 60×27	м	194,45	1, 2, 3, 4, 5, 6, 7
Профиль ПН 28×27	м	104,41	1, 2, 3, 4, 5, 6, 7
Подвес прямой	шт.	61	1, 2, 3, 4, 5, 6, 7
Анкер-клин к плите	шт.	61	1, 2, 3, 4, 5, 6, 7
Шуруп TN 3,5×25	шт.	1581	1, 2, 3, 4, 5, 6, 7
Лента армирующая для швов	м	82,46	1, 2, 3, 4, 5, 6, 7
Шпаклёвка для швов	кг	27,49	1, 2, 3, 4, 5, 6, 7
Грунтовка (швы)	л	6,87	1, 2, 3, 4, 5, 6, 7
Лента разделительная по периметру	м	87,03	1, 2, 3, 4, 5, 6, 7
Сплошная шпаклёвка и окраска (площадь развёртки)	м²	68,72	1, 2, 3, 4, 5, 6, 7

Допущения и предложения на листе

Основа листа: планировка по обводу плана заказчика, не замерена (К-1); высота до плиты 2650 мм от чистого пола — решение автора (ИЗ-1); отметки плана потолков сдвинуты на -95 мм (+2.745 плана = низ плиты), не замерено (К-2); толщины стен приняты: наружные 260 мм, перегородки 130 мм (К-1); положение стен и проёмов — по брифу без обмера и плана БТИ (К-1); разрешённая мощность 10 кВт принята, ТУ не переданы (К-6); вентканалы приняты, в брифе не заданы (К-5); тип дома, перекрытие и несущие стены не известны — документов нет (К-3); плита электрическая — принята, в брифе не указано (К-6); система заземления TN-C-S принята, ТУ не переданы (К-6); число жильцов 2 принято, в брифе не указано (К-9); подрайон климата не задан — принят не северный (жилые от 2,5 м) (К-26).

См. лист открытых вопросов (лист 5, записи К-1, К-3, К-5, К-6, К-9; лист 6, запись К-26).

Примечания

1. ГКЛ 12,5 мм по каркасу П113; узлы коробов и ниш под шторы: узел 1 — лист 46; условные обозначения разрезов — на листе 46.
2. Ведомость объёмов — по геометрии плана потолков: Лист ГКЛ 12,5 — плоскости уровней + борта (без арочных участков); Лист ГКЛВ 12,5 — плоскости уровней + борта; Борта и карнизы — длина перепада × перепад; Профиль ПП 60×27 — S × (1/шаг несущ. + 1/шаг осн.) + стойки бортов; Профиль ПН 28×27 — периметр стен + 2 × перепады + карнизы; Подвес прямой — по раскладке: S уровня / (шаг осн. × шаг подвесов), пояс уже шага — ряд вдоль пояса, фигура — по контуру; шаг подвесов — не больше табл. 14 СП 163; Анкер-клин к плите — по одному на подвес (Knauf П113); Шуруп TN 3,5×25 — 23 шт./м² (Knauf П113, табл. 2 альбома П 11); Лента армирующая для швов — 1,2 м/м² листа (Knauf); Шпаклёвка для швов — 0,4 кг/м² листа, только швы (Knauf); Грунтовка (швы) — 0,1 л/м² листа, только швы (Knauf); Лента разделительная по периметру — периметр стен под потолком ГКЛ; Сплошная шпаклёвка и окраска (площадь развёртки) — плоскости + борта; расход — по паспорту материала (норма расхода на сплошной слой не подтверждена); без запаса на подрезку (при закупке листа: ×1,075 при S > 20 м², ×1,175 — 10–20 м², ×1,275 — < 10 м²).

Изм.	Кол.уч	Лист	№ док.	Подп.	Дата
Разраб.		Кырлан А.С.			04.11.26
Пров.					
ГИП					
Н. контр.					
Утв.					

ГД-2026-020-АИ

Квартира 68 м², элитный модерн

Общая площадь 68,47* м² · * размеры приняты, не замерены (реестр — л. 5–7, К-1)

Дизайн-проект интерьера

Стадия	Лист	Листов
РП	47	105

Разрезы и узлы потолков (продолжение)

М б/м

Кырлан Александр Сергеевич

выпуск 04.11.2026 № 8be4ef4c81 · стр. 53 из 117


Сечения потолков М 1:10

ПРЕДВАРИТЕЛЬНО · не для производства работ · открыто пунктов: 25 (реестр — л. 5–7)

Пом. 5, 7 · профили, подвесы, крепёж, изделия · размеры в мм

Сечение 5.1. Ниша под шторы (М 1:10)

Пом. 5 Кухня-столовая, 7 Спальня; без подсветки; закладные под карниз — до обшивки

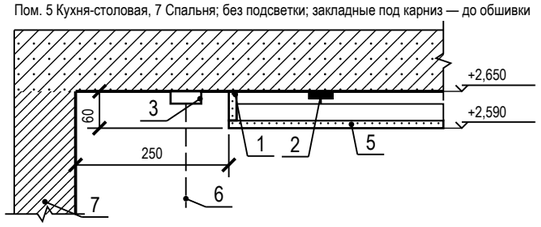

1 — стенка ниши — ГКЛ 12,5

2 — анкер-клин к плите — по одному на подвес; подвес прямой, шаг 1000 мм

3 — карниз (шина), высота с верхом портьеры 60 мм

4 — ПП 60×27 — каркас короба, основные через 1200 мм; соединители одноуровневые, шурупы LN 3,5×9


5 — низ короба нижнего уровня — ГКЛ 12,5; шурупы TN 3,5×25 через 170 мм

6 — портьера

7 — стена с окном

Сечение 5.2. Примыкание потолка к стене (М 1:10)

Пом. 5 Кухня-столовая, 7 Спальня; примыкание — теневой шов

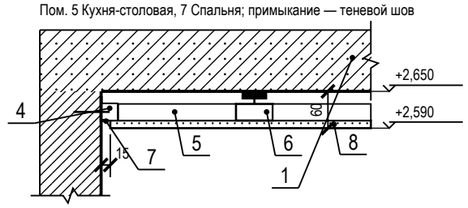

1 — плита перекрытия

2 — анкер-клин к плите — по одному на подвес

3 — подвес прямой, шаг 1000 мм

4 — ПН 28×27 по периметру — дюбель-гвоздь через ≤ 500 мм, не менее 3 на профиль

5 — ПП 60×27 несущий (вид) через 500 мм, в ПН

6 — ПП 60×27 основной (сечение) через 1200 мм; соединители одноуровневые, шурупы LN 3,5×9

7 — теневой профиль: шов 15 мм, зазор 3 мм; стена под шов выровнена

8 — ГКЛ 12,5 по П113; шурупы TN 3,5×25 через 170 мм

Допущения и предложения на листе

Основа листа: планировка по обводу плана заказчика, не замерена (К-1); высота до плиты 2650 мм от чистого пола — решение автора (ИЗ-1); отметки плана потолков сдвинуты на -95 мм (+2.745 плана = низ плиты), не замерено (К-2); толщины стен приняты: наружные 260 мм, перегородки 130 мм (К-1); положение стен и проёмов — по брифу без обмера и плана БТИ (К-1); разрешённая мощность 10 кВт принята, ТУ не переданы (К-6); вентканалы приняты, в брифе не заданы (К-5); тип дома, перекрытие и несущие стены не известны — документов нет (К-3); плита электрическая — принята, в брифе не указано (К-6); система заземления TN-C-S принята, ТУ не переданы (К-6); число жильцов 2 принято, в брифе не указано (К-9); подрайон климата не задан — принят не северный (жилые от 2,5 м) (К-26).

См. лист открытых вопросов (лист 5, записи К-1, К-3, К-5, К-6, К-9; лист 6, запись К-26).

Примечания

1. Сечения потолков М 1:10 по помещениям с нишами LED и нишами под шторы: отметки и размеры этого помещения от ±0,000 чистого пола (м, мм). Положение — по плану потолков (лист 45): короб и ниша LED — по линиям ленты, ниша под шторы — у стены с окном; типовые узлы по группам помещений — на листе 46.
2. Крепёж: подвес прямой к плите на анкер-клине — по одному на подвес (Knauf П113); ПН к стенам — дюбель-гвоздь через ≤ 500 мм, не менее 3 на профиль (серия 1.045.9-2.08); лист 12,5 — шурупы TN 3,5×25 через 170 мм (СП 163, табл. 15); профили между собой — соединители одноуровневые, шурупы LN 3,5×9.
3. Изделие карниза, профиля LED и галтели подписано артикулом из данных; где артикул не выбран, сечение дано по габаритам из данных (ширина и глубина ниши, щель под свет), изделие подбирается по ним.

1000 мм · печать 1:1

Изм.	Кол.уч	Лист	№ док.	Подп.	Дата
Разраб.		Кырлан А.С.			04.11.26
Пров.					
ГИП					
Н. контр.					
Утв.					

ГД-2026-020-АИ

Квартира 68 м², элитный модерн

Общая площадь 68,47* м² · * размеры приняты, не замерены (реестр — л. 5–7, К-1)

Дизайн-проект интерьера

Стадия	Лист	Листов
РП	48	105

Сечения потолков М 1:10

М 1:10

Кырлан Александр Сергеевич


выпуск 04.11.2026 № 8be4ef4c81 · стр. 54 из 117

Раскладка плитки. Планы полов


Раскладка от чистовых размеров · размеры в мм · отметки от ±0,000

ПРЕДВАРИТЕЛЬНО · не для производства работ · открыто пунктов: 25 (реестр — л. 5–7)


Фрагмент 1. Санузел (пом. 2). Пол 600×600, шов 2 мм, М 1:50

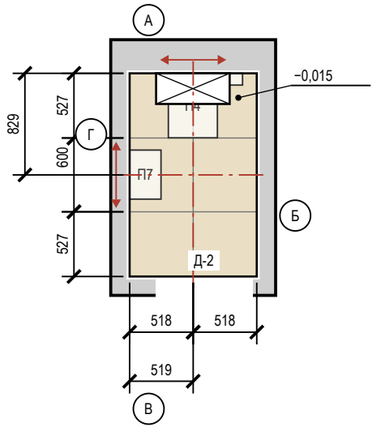

Фрагмент 2. Ванная (пом. 3). Пол 600×600, шов 2 мм, М 1:50

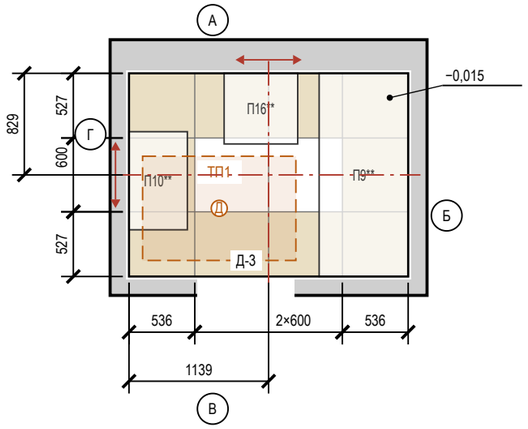

Фрагмент 3. Прихожая (пом. 4). Пол 600×1200, шов 2 мм, М 1:50

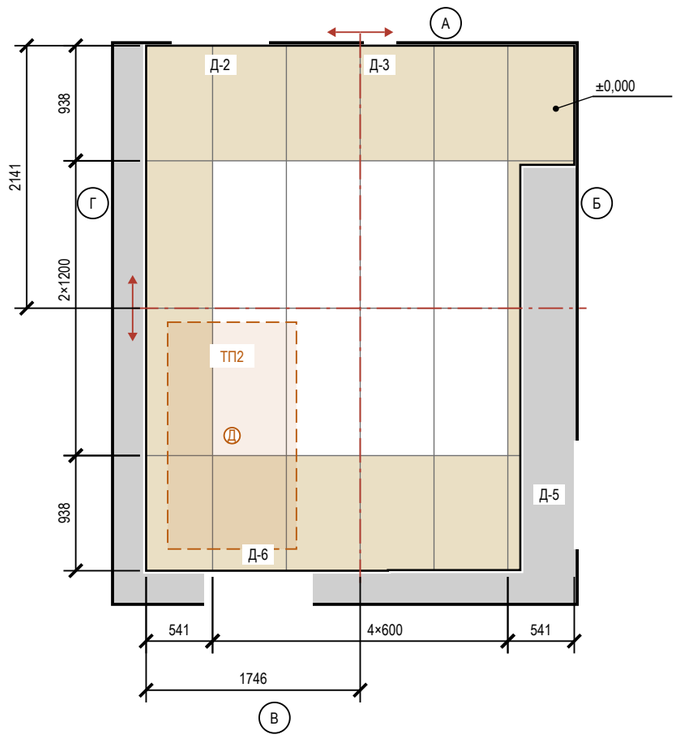

Условные обозначения

- плитка целая; тонкая линия — шов
- плитка с подрезкой (размер — на цепочке)
- ось старта; стрелки — направление укладки
- сантехприбор: габарит, высота по практике
- короб инсталляции: плитка пола — до короба
- электрический тёплый пол: контур мата ТП, Д — датчик
- отметка чистого пола на полке выноски, м
- А — обозначение стены А–Г (как на развёртках)

Примечания

1. Раскладка от чистовых размеров: стены санузлов теряют 10 + 5 + 9 = 24 мм на сторону (штукатурка, клей, плитка); подрезки — чистые, без шва.
2. Старт — от центра помещения (штрихпунктир, стрелки — направление укладки); размер старта — от чистовых стен Г и А.
3. Раскладка фартука «Кухня-столовая» — на листе «Раскладка плитки. Фартук кухни».
4. Калибр партии не задан — до укладки замерить (рабочий размер W, ГОСТ 13996-2019) и пересчитать подрезки.
5. Количество: целые по раскладке + по одной на подрезку, запас 10 %; один артикул — одна партия и тон. Исключены поддон, короб, проёмы и места за коробом; S — по чистым граням: стены нетто = зона облицовки по ведомости отделки − место за коробом инсталляции 0,72 м² (плитку за коробом не кладут), короб — отдельной строкой.
6. Клей C2 TE S1 Ceresit CM 17; C2 TE S1 (ГОСТ Р 56387-2018), затирка CG2WA Mapei Ultracolor Plus 132; CG2WA; расход — по ТУ выбранной марки.
7. Гидроизоляция: пол и стены 200 мм от ЧП; над ванной — до 2000 и 300 мм за борт (пом. 3) (см. развёртки); акт скрытых работ, пролив 24 ч.
8. Электрический тёплый пол: ТП1 — пом. 3, мат 1250×850 мм, 160 Вт; ТП2 — пом. 4, мат 1050×1850 мм, 290 Вт; контуры показаны пунктиром; датчик температуры (Д) — в гофротрубе, трасса к терморегулятору — по обмеру. Марка мата и точное положение датчика — при закупке и по обмеру. Плитку над матом клеить клеем, который изготовитель допускает для тёплого пола, до включения выдержать срок по ТУ клея.
9. Швы пола совмещены со швами стены А; по периметру — демпферная лента.
10. Отметка чистого пола −0,015, порог 15 мм; стык с соседним покрытием — по оси полотна двери.

Ведомость плитки

Помещение, поверхность	Плитка, код	Формат	Шов	S, м²	Целых	Подр.	С запасом
Санузел, пол	аналог: керамогранит под травертин	600×600	2	1,85	0	6	7
Санузел, стены А–Г	аналог: керамогранит под травертин	600×1200	2	11,04	4	16	24
Санузел, короб инсталляции	аналог: керамогранит под травертин	600×1200	2	1,47	1	3	5
Ванная, пол	аналог: керамогранит под травертин	600×600	2	3,96	2	10	14
Ванная, стены А–Г	аналог: керамогранит под травертин	600×1200	2	17,72	8	20	32
Прихожая, пол	аналог: керамогранит ректифицированный под травертин, матовый	600×1200	2	13,87	8	16	27
Кухня-столовая, фартук (ст. А)	аналог: керамогранит под травертин, матовый	1200×600	2	1,68	0	5	6
Итого 600×600				5,81	2	16	21
Итого 600×1200				**45,78**	**21**	**60**	**94**

Ведомость материалов

Материал	Класс, код	Норма расхода	Кол-во
Затирка	CG2WA Mapei Ultracolor Plus 132	(a+b)/ab·шов·t·1,6	4,0 кг
Затирка	CG2WA	(a+b)/ab·шов·t·1,6	0,1 кг
Клей	C2 TE S1 Ceresit CM 17	1,5 кг/м²·мм, слой 5	398 кг (16 меш.)
Клей	C2 TE S1	1,5 кг/м²·мм, слой 5	14 кг (1 меш.)
Гидроизоляция	обмазочная, 2 слоя: пол, стены по периметру и зоны замачивания	по ТУ	15,8 м²
Демпф. лента	по периметру пола из плитки		26,9 м

Допущения и предложения на листе

Основа листа: планировка по обводу плана заказчика, не замерена (К-1); высота до плиты 2650 мм от чистого пола — решение автора (ИЗ-1); отметки плана потолков сдвинуты на -95 мм (+2.745 плана = низ плиты), не замерено (К-2); толщины стен приняты: наружные 260 мм, перегородки 130 мм (К-1); положение стен и проёмов — по брифу без обмера и плана БТИ (К-1); разрешённая мощность 10 кВт принята, ТУ не переданы (К-6); вентканалы приняты, в брифе не заданы (К-5); тип дома, перекрытие и несущие стены не известны — документов нет (К-3); плита электрическая — принята, в брифе не указано (К-6); система заземления TN-C-S принята, ТУ не переданы (К-6); число жильцов 2 принято, в брифе не указано (К-9); подрайон климата не задан — принят не северный (жилые от 2,5 м) (К-26).

Знак «**» — предложение проектировщика, заказчиком не утверждено (согласовать с заказчиком): ИЗ-3, К-7: П10 — раковина у левой стены: светильники 14 плана — у зеркала над ней; отвод К1 к стояку в углу короткий; П16 — место стиральной машины — в ванной у верхней стены, правее короба стояка; подход 1100 мм перед дверцей, выводы ХВС и К1 Ø40 за машиной; ИЗ-3, К-28: П9 — ванна 1700 × 750 у правой стены на всю глубину помещения (1700 мм по плану) — стояк в левом углу свободен; К-8: пол пом. 2, 3 — пирог пола: стяжка 33 мм и обмазочная гидроизоляция добавлены разработчиком проекта; артикул изделия не выбран: позиция описана характеристиками («аналог по характеристикам»), артикул выбирается при закупке; стены пом. 2, 3, пол пом. 4, плинтус пом. 4 — артикул изделия не выбран: позиция описана характеристиками («аналог по характеристикам»), артикул выбирается при закупке.

См. лист открытых вопросов (лист 5, записи К-1, К-3, К-5–К-9; лист 6, запись К-26; лист 7, записи ИЗ-3, К-28).

1000 мм · печать 1:1

Изм.	Кол.уч	Лист	№ док.	Подп.	Дата
Разраб.		Кырлан А.С.			04.11.26
Пров.					
ГИП					
Н. контр.					
Утв.					

ГД-2026-020-АИ

Квартира 68 м², элитный модерн

Общая площадь 68,47* м² · * размеры приняты, не замерены (реестр — л. 5–7, К-1)

Дизайн-проект интерьера

Стадия	Лист	Листов
РП	49	105

Раскладка плитки. Планы полов

М 1:50

Кырлан Александр Сергеевич


выпуск 04.11.2026 № 8be4ef4c81 · стр. 55 из 117

Раскладка плитки. Фартук кухни

ПРЕДВАРИТЕЛЬНО · не для производства работ · открыто пунктов: 25 (реестр — л. 5–7)

Раскладка от чистовых размеров · размеры в мм · высоты фартука от чистого пола

Фрагмент 1. Кухня-столовая (пом. 5), фартук, стена А. 1200×600, шов 2 мм, М 1:20

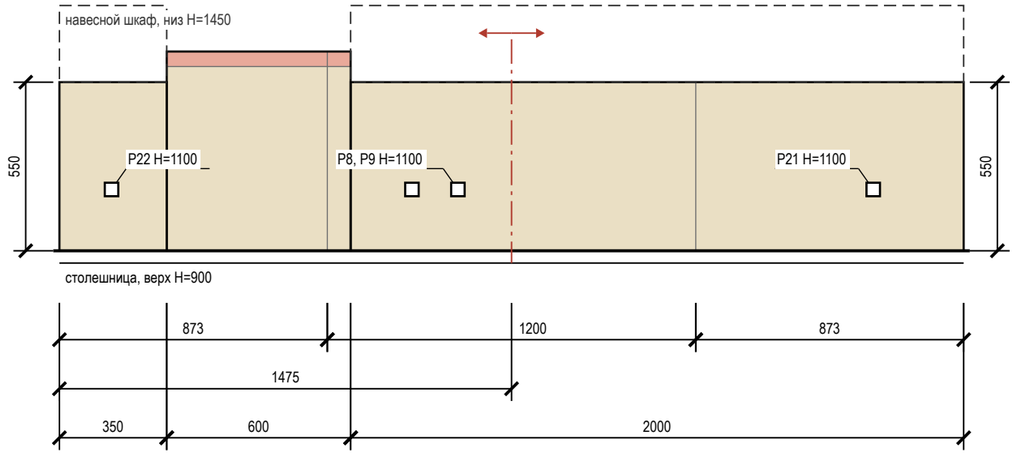

Условные обозначения

- плитка целая; тонкая линия — шов
- плитка с подрезкой (размер — на цепочке)
- ось старта; стрелки — направление укладки
- электроточка: марка и H — по листам ЭОМ
- столешница (верх)
- навесной шкаф над фартуком

Подсчёт плитки

Поверхность	Формат	S, м²	Целых	Подр.	С запасом
Кухня-столовая, фартук (ст. А)	1200×600	1,68	0	5	6

Сдвиг розеток фартука под раскладку

Точка (ЭОМ)	Сейчас: от края фартука / H	Под раскладку: от края / H	Сдвиг, мм
P8, P9, P22	1150, 1300, 170 / 1100	1150, 1300, 170 / 1175	H +75 — ось ряда
P21	2655 / 1100	2655 / 1175	H +75 — ось ряда

Примечания

1. Фартук, Кухня-столовая: 1200×600 горизонтально, шов 2 мм; зоны 350 мм — 900…1450, 600 мм — 900…1550, 2000 мм — 900…1450 (от столешницы до низа навесного шкафа, без шкафа — 650 мм). Старт от центра участка, подрезки 873 мм. Площадь 1,68 м² — как в ведомости отделки.
2. Фартук — после монтажа столешницы, низ на 2–3 мм выше неё, шов со столешницей — санитарный герметик; навесные шкафы — после фартука. Торцы у пенала и стены — профиль или запил 45°.
3. Фартук, Кухня-столовая: в зоне до отм. 1550 верхний ряд подрезан 48 мм — меньше 1/3 плитки; полоса прикрыта корпусом навесного модуля и на виду не остаётся. Раскладкой не снимается: убрать подрезку можно, только выровняв низ этого модуля с соседними (1450 мм) — решение мебельщика.
4. Розетки из таблицы переносятся до черновой электрики: по высоте — на ось ряда плитки, от вертикального шва крупной плитки — не ближе 60 мм. Привязка — от левого края фартука на развёртке.
5. Клей, затирка и итог по форматам — в ведомостях листа «Раскладка плитки. Планы полов».

Допущения и предложения на листе

Основа листа: планировка по обводу плана заказчика, не замерена (К-1); высота до плиты 2650 мм от чистого пола — решение автора (ИЗ-1); отметки плана потолков сдвинуты на -95 мм (+2.745 плана = низ плиты), не замерено (К-2); толщины стен приняты: наружные 260 мм, перегородки 130 мм (К-1); положение стен и проёмов — по брифу без обмера и плана БТИ (К-1); разрешённая мощность 10 кВт принята, ТУ не переданы (К-6); вентканалы приняты, в брифе не заданы (К-5); тип дома, перекрытие и несущие стены не известны — документов нет (К-3); плита электрическая — принята, в брифе не указано (К-6); система заземления TN-C-S принята, ТУ не переданы (К-6); число жильцов 2 принято, в брифе не указано (К-9); подрайон климата не задан — принят не северный (жилые от 2,5 м) (К-26).

Знак «**» — предложение проектировщика, заказчиком не утверждено (согласовать с заказчиком): К-7: акцент пом. 5; К-8: пол пом. 5, плинтус пом. 5, фартук пом. 5 — артикул изделия не выбран: позиция описана характеристиками («аналог по характеристикам»), артикул выбирается при закупке.

См. лист открытых вопросов (лист 5, записи К-1, К-3, К-5–К-9; лист 6, запись К-26).

1000 мм · печать 1:1

Изм.	Кол.уч	Лист	№ док.	Подп.	Дата
Разраб.		Кырлан А.С.			04.11.26
Пров.					
ГИП					
Н. контр.					
Утв.					

ГД-2026-020-АИ

Квартира 68 м², элитный модерн

Общая площадь 68,47* м² · * размеры приняты, не замерены (реестр — л. 5–7, К-1)

Дизайн-проект интерьера

Стадия	Лист	Листов
РП	50	105

Раскладка плитки. Фартук кухни

М 1:20


Кырлан Александр Сергеевич


выпуск 04.11.2026 № 8be4ef4c81 · стр. 56 из 117

Раскладка плитки. Санузел. Развёртки стен

ПРЕДВАРИТЕЛЬНО · не для производства работ · открыто пунктов: 25 (реестр — л. 5–7)

Пом. 2 · вид изнутри помещения · размеры в мм · высоты от чистого пола, отметки от ±0,000

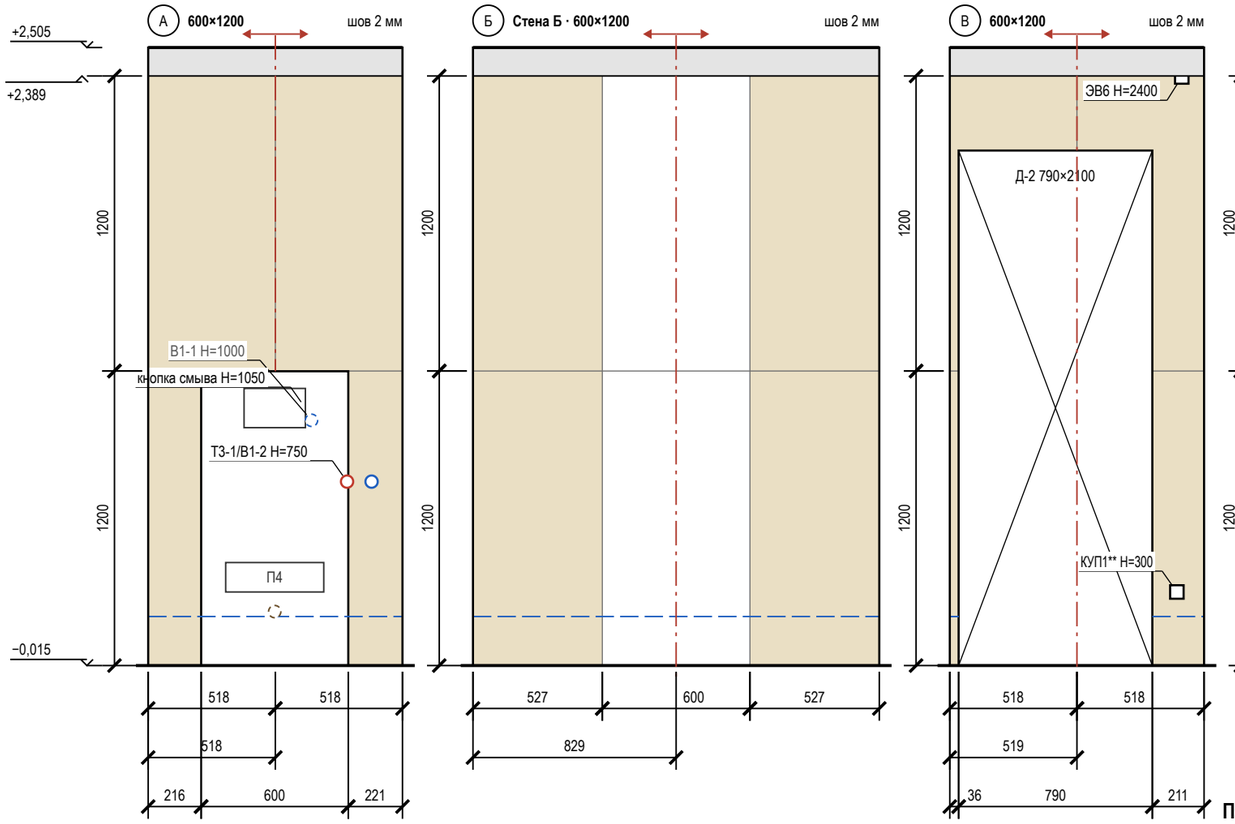

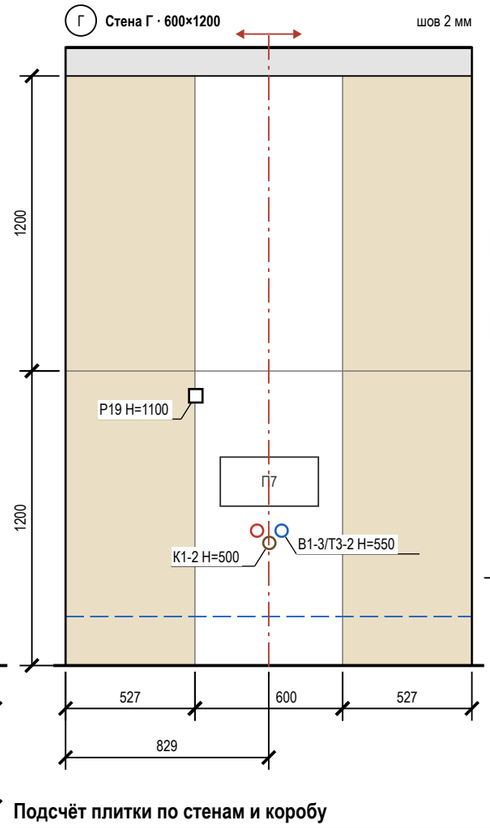

Условные обозначения

- плитка целая; тонкая линия — шов
- плитка с подрезкой (размер — на цепочке)
- ось старта; стрелки — направление укладки
- верх гидроизоляции: 200 от ЧП, в мокрой зоне — «до …»
- проём — не облицовывается
- сантехприбор: габарит, высота по практике
- короб инсталляции, в нём кнопка смыва 250×160
- вывод В1 (код — в ведомости привязок)
- вывод Т3 (код — в ведомости привязок)
- вывод К1 (код — в ведомости привязок)
- вывод за прибором / в коробе (не на сетке)
- электроточка: марка и Н — по листам ЭОМ
- отметка уровня, м: ±0,000 — чистый пол жилых помещений
- низ потолка; серая полоса — стена без плитки
- А обозначение стены А–Г (как на развёртках)

Подсчёт плитки по стенам и коробу

Поверхность	L × H, мм	S, м²	Целых	Подр.	С запасом	Подрезки: край / верх, мм
стена А	1037 × 2404	1,89	0	4	5	518 / 518; целый ряд
короб (ст. А)	600×1200×250	1,47	1	3	5	лицо 600; бок. 250
стена Б	1657 × 2404	4,10	2	4	7	527 / 527; целый ряд
стена В	1037 × 2404	0,95	0	4	5	518 / 518; целый ряд
стена Г	1657 × 2404	4,10	2	4	7	527 / 527; целый ряд
Итого		**12,51**	**5**	**19**	**29**	

Сдвиг точек под раскладку

Точка (ВК, ЭОМ)	Стена	Проект: от угла / Н	Под раскладку: от угла / Н	Сдвиг, мм
ЭВ6	В	946 / 2400	819 / 2400	−127 в центр плитки
КУП1**	В	926 / 300	819 / 300	−107 в центр плитки

Допущения и предложения на листе

Основа листа: планировка по обводу плана заказчика, не замерена (К-1); высота до плиты 2650 мм от чистого пола — решение автора (ИЗ-1); отметки плана потолков сдвинуты на -95 мм (+2.745 плана = низ плиты), не замерено (К-2); толщины стен приняты: наружные 260 мм, перегородки 130 мм (К-1); положение стен и проёмов — по брифу без обмера и плана БТИ (К-1); разрешённая мощность 10 кВт принята, ТУ не переданы (К-6); вентканалы приняты, в брифе не заданы (К-5); тип дома, перекрытие и несущие стены не известны — документов нет (К-3); плита электрическая — принята, в брифе не указано (К-6); система заземления TN-C-S принята, ТУ не переданы (К-6); число жильцов 2 принято, в брифе не указано (К-9); подрайон климата не задан — принят не северный (жилые от 2,5 м) (К-26).

Знак «**» — предложение проектировщика, заказчиком не утверждено (согласовать с заказчиком): КУП1 — коробка уравнивания потенциалов, проводник от шины РЕ; К-1: дверь пом. 2 (стена В) — проём принят по обводу плана заказчика, без обмера: положение и ширина сняты с плана, не замерены; открывание наружу (в прихожую): санузел 1,1 м — внутрь полотно задевает раковину П14; К-8: пол пом. 2 — пирог пола: стяжка 33 мм и обмазочная гидроизоляция добавлены разработчиком проекта; артикул изделия не выбран: позиция описана характеристиками («аналог по характеристикам»), артикул выбирается при закупке; стены пом. 2 — артикул изделия не выбран: позиция описана характеристиками («аналог по характеристикам»), артикул выбирается при закупке.

См. лист открытых вопросов (лист 5, записи К-1, К-3, К-5, К-6, К-8, К-9; лист 6, запись К-26).

Примечания

1. Вид изнутри, стены по часовой стрелке А → Г. Высоты — от чистого пола (−0,015), отметки — от ±0,000. Раскладка от чистовых размеров (штукатурка 10 + клей 5 + плитка 9 мм), подрезки чистые; старт — от оси стены, ряды от пола целыми.
2. Верх плитки +2,389, потолок +2,505, зазор 116 мм: потолок ГКЛ опустить до +2,392 (шов 3 мм, герметик) — согласовать с монтажником ГКЛ; иначе профиль-окантовка, полосу окрасить в цвет потолка. Подрезной ряд 111 мм не делать.
3. Точки из таблицы сдвигов переносятся до черновой разводки (ЭОМ — по тем же числам).
4. Выводы ВК стоят по оси прибора и с прибором не двигаются — привязки по «Плану выводов сантехники» без сдвига; вне сетки (Т3-1/В1-2) — отверстие в плитке коронкой по той же привязке, плитку не сдвигать.
5. Выводы — по «Плану выводов сантехники», электроточки — по ЭОМ, «*» — высота по практике; за приборами и в коробе (В1-1, К1-1) — штриховым кольцом.
6. Гидроизоляция: 200 мм от ЧП по периметру; углы — лентой; акт скрытых работ, пролив.
7. Короб 600×1200×250: лицо 600 мм от оси кнопки смыва, боковины, полка; углы — запил 45° или профиль; за коробом плитку не кладут.

1000 мм · печать 1:1

Изм.	Кол.уч	Лист	№ док.	Подп.	Дата
Разраб.		Кырлан А.С.			04.11.26
Пров.					
ГИП					
Н. контр.					
Утв.					

ГД-2026-020-АИ

Квартира 68 м², элитный модерн

Общая площадь 68,47* м² · * размеры приняты, не замерены (реестр — л. 5–7, К-1)

Дизайн-проект интерьера

Стадия	Лист	Листов
РП	51	105

Раскладка плитки. Санузел. Развёртки стен

М 1:25


Кырлан Александр Сергеевич

выпуск 04.11.2026 № 8be4ef4c81 · стр. 57 из 117

Раскладка плитки. Ванная. Развёртки стен

ПРЕДВАРИТЕЛЬНО · не для производства работ · открыто пунктов: 25 (реестр — л. 5–7)

Пом. 3 · вид изнутри помещения · размеры в мм · высоты от чистого пола, отметки от ±0,000

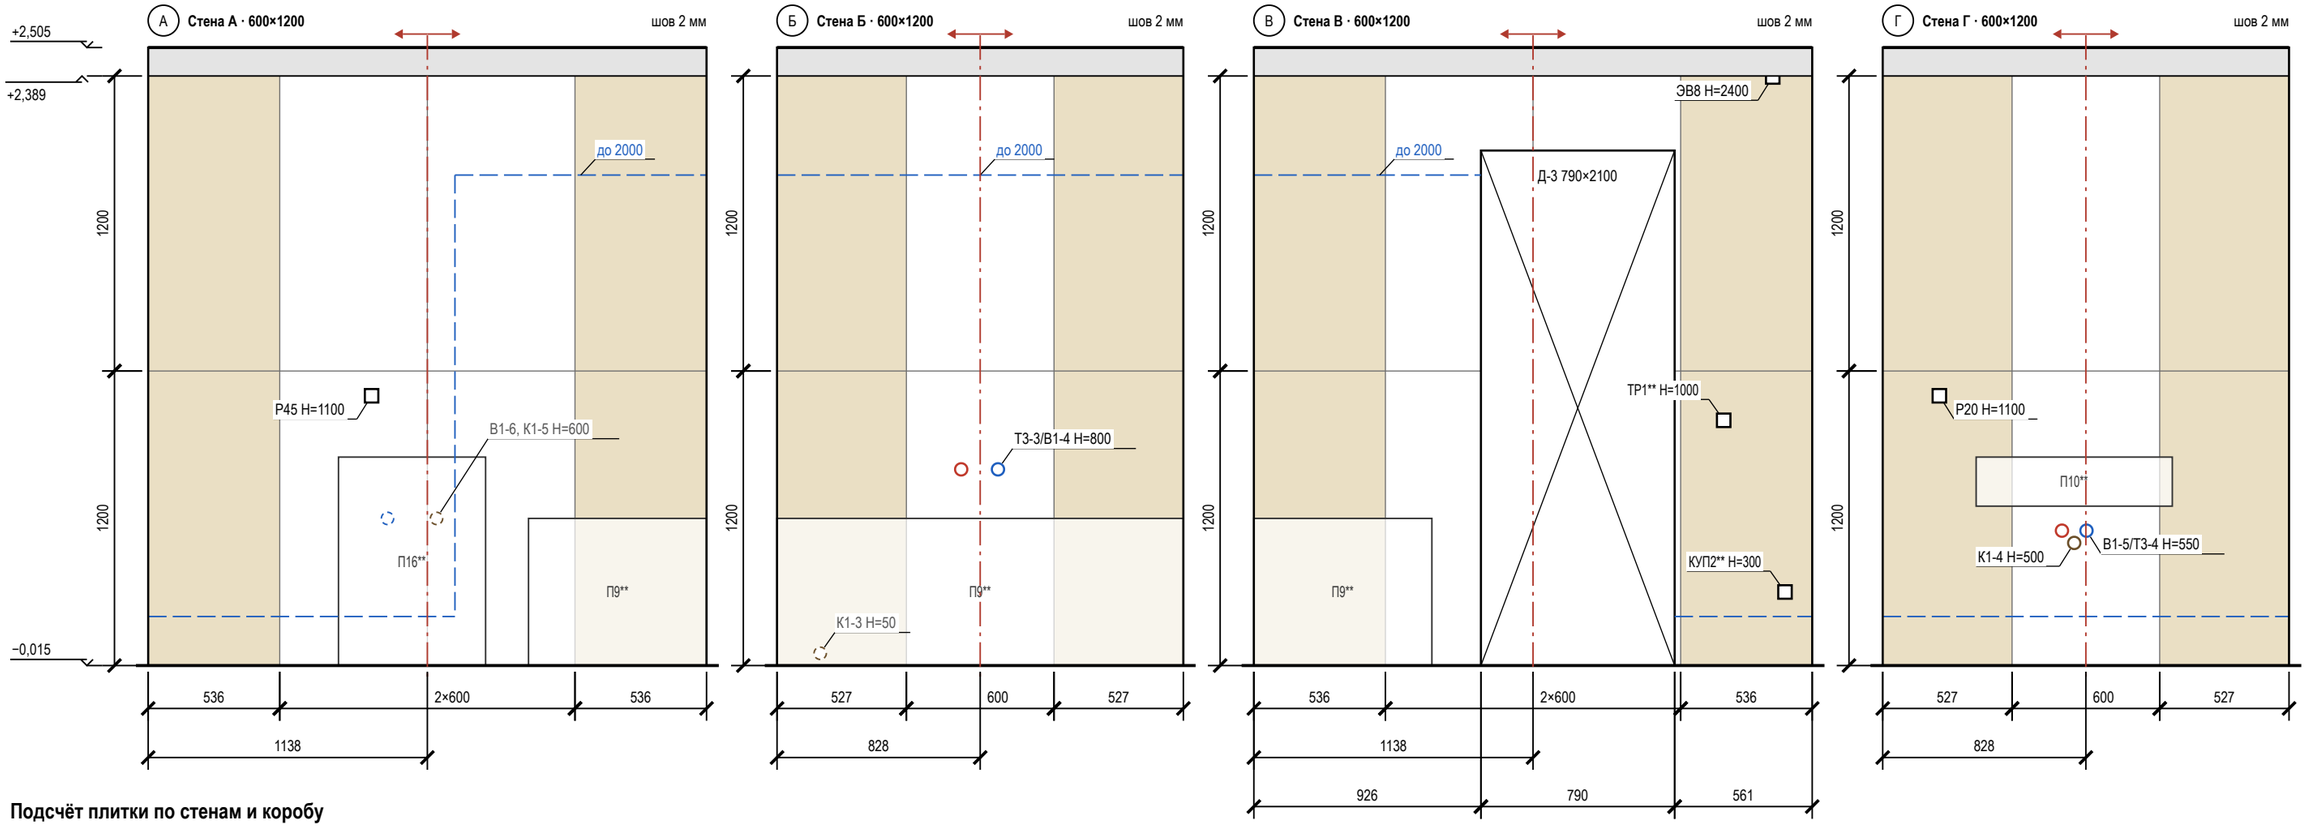

Подсчёт плитки по стенам и коробу

Поверхность	L × H, мм	S, м²	Целых	Подр.	С запасом	Подрезки: край / верх, мм
стена А	2277 × 2404	5,59	4	4	9	536 / 536; целый ряд
стена Б	1657 × 2404	4,10	2	4	7	527 / 527; целый ряд
стена В	2277 × 2404	3,93	0	8	9	536 / 536; целый ряд
стена Г	1657 × 2404	4,10	2	4	7	527 / 527; целый ряд
Итого		**17,72**	**8**	**20**	**32**	

Сдвиг точек под раскладку

Точка (ВК, ЭОМ)	Стена	Проект: от угла / H	Под раскладку: от угла / H	Сдвиг, мм
Р45	А	911 / 1100	838 / 1100	−73 в центр плитки
ЭВ8	В	2116 / 2400	2041 / 2400	−75 в центр плитки
КУП2**	В	2166 / 300	2041 / 300	−125 в центр плитки
ТР1**	В	1916 / 1000	2041 / 1000	+125 в центр плитки

Примечания

1. Вид изнутри, стены по часовой стрелке А → Г. Высоты — от чистого пола (−0,015), отметки — от ±0,000. Раскладка от чистовых размеров (штукатурка 10 + клей 5 + плитка 9 мм), подрезки чистые; старт — от оси стены, ряды от пола целыми.
2. Верх плитки +2,389, потолок +2,505, зазор 116 мм: потолок ГКЛ опустить до +2,392 (шов 3 мм, герметик) — согласовать с монтажником ГКЛ; иначе профиль-окантовка, полосу окрасить в цвет потолка. Подрезной ряд 111 мм не делать.
3. Точки из таблицы сдвигов переносятся до черновой разводки (ЭОМ — по тем же числам).
4. Выводы ВК стоят по оси прибора и с прибором не двигаются — привязки по «Плану выводов сантехники» без сдвига; вне сетки (В1-5/Т3-4, К1-4) — отверстие в плитке коронкой по той же привязке, плитку не сдвигать.
5. Выводы — по «Плану выводов сантехники», электроточки — по ЭОМ, «*» — высота по практике; за приборами и в коробе (В1-6, К1-5, К1-3) — штриховым кольцом.
6. Гидроизоляция: 200 мм от ЧП по периметру; над ванной — до 2000 и 300 мм за борт (СП 29.13330.2011, п. 7.2 — на высоту замачивания); углы — лентой; акт скрытых работ, пролив.

1000 мм · печать 1:1

Условные обозначения

- плитка целая; тонкая линия — шов
- плитка с подрезкой (размер — на цепочке)
- ось старта; стрелки — направление укладки
- верх гидроизоляции: 200 от ЧП, в мокрой зоне — «до …»
- проём — не облицовывается
- сантехприбор: габарит, высота по практике
- вывод В1 (код — в ведомости привязок)
- вывод Т3 (код — в ведомости привязок)
- вывод К1 (код — в ведомости привязок)
- вывод за прибором / в коробе (не на сетке)
- электроточка: марка и H — по листам ЭОМ
- отметка уровня, м: ±0,000 — чистый пол жилых помещений
- низ потолка; серая полоса — стена без плитки
- (А) обозначение стены А–Г (как на развёртках)

Допущения и предложения на листе. Основа листа: планировка по обводу плана заказчика, не замерена (К-1); высота до плиты 2650 мм от чистого пола — решение автора (ИЗ-1); отметки плана потолков сдвинуты на -95 мм (+2.745 плана = низ плиты), не замерено (К-2); толщины стен приняты: наружные 260 мм, перегородки 130 мм (К-1); положение стен и проёмов — по брифу без обмера и плана БТИ (К-1); разрешённая мощность 10 кВт принята, ТУ не переданы (К-6); вентканалы приняты, в брифе не заданы (К-5); тип дома, перекрытие и несущие стены не известны — документов нет (К-3); плита электрическая — принята, в брифе не указано (К-6); система заземления TN-C-S принята, ТУ не переданы (К-6); число жильцов 2 принято, в брифе не указано (К-9); подрайон климата не задан — принят не северный (жилые от 2,5 м) (К-26). Знак «*» — принято, не замерено (замерить): К-1: дверь пом. 3 (стена В). Знак «**» — предложено, не утверждено (согласовать): ТР1, КУП2; ИЗ-3, К-7: П10, П16; ИЗ-3, К-28: П9; К-8: пол пом. 3, стены пом. 3. См. лист открытых вопросов (лист 5, записи К-1, К-3, К-5–К-9; лист 6, запись К-26; лист 7, записи ИЗ-3, К-28).

Изм.	Кол.уч	Лист	№ док.	Подп.	Дата
Разраб.		Кырлан А.С.			04.11.26
Пров.					
ГИП					
Н. контр.					
Утв.					

ГД-2026-020-АИ

Квартира 68 м², элитный модерн

Общая площадь 68,47* м² · * размеры приняты, не замерены (реестр — л. 5–7, К-1)

Дизайн-проект интерьера

Стадия	Лист	Листов
РП	52	105

Раскладка плитки. Ванная. Развёртки стен

М 1:25

Кырлан Александр Сергеевич

выпуск 04.11.2026 № 8be4ef4c81 · стр. 58 из 117

07

Полы и отделка

Кырлан Александр Сергеевич


выпуск 04.11.2026 № 8be4ef4c81 · стр. 59 из 117

План полов

Покрытия, направление укладки, отметки чистого пола, стыки · размеры в мм · отметки в м

ПРЕДВАРИТЕЛЬНО · не для производства работ · открыто пунктов: 25 (реестр — л. 5–7)

Допущения и предложения на листе. Знак «*» принято (замерить): дверь пом. 3 (стена В), 5 (Г), Ст К1-1, Ст В1-2, Ст Т3-3. Знак «**» предложено (согласовать): пол пом. 1–7, плинтус пом. 1, 4–7, акцент пом. 1, 5–7, стены пом. 2, 3, фартук пом. 5, дверь пом. 2 (стена В). См. лист открытых вопросов (листы 5–7).

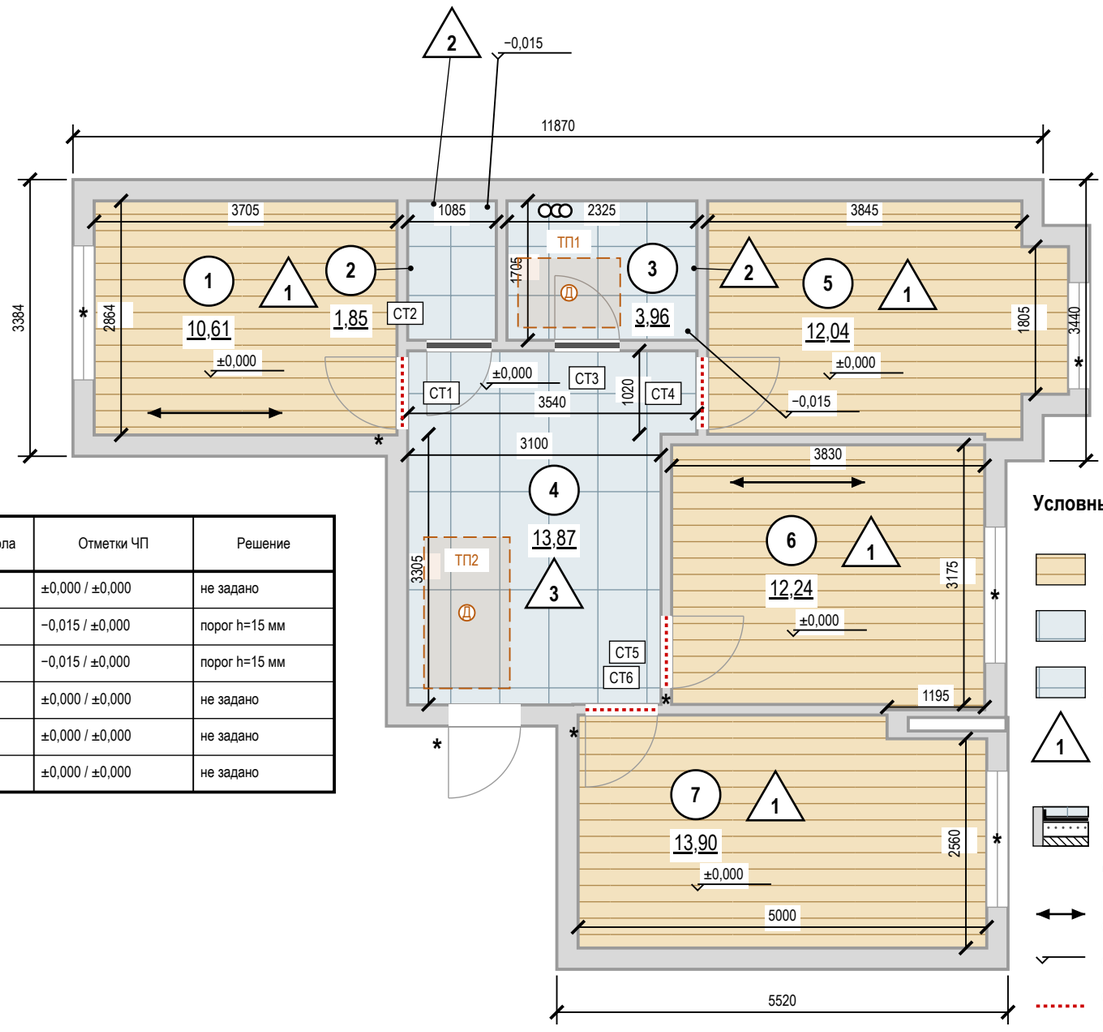




Стыки покрытий в проёмах

Марка	Проём	Типы пола	Отметки ЧП	Решение
СТ1	1–4 (Д-1)	1 / 3	±0,000 / ±0,000	не задано
СТ2	2–4 (Д-2)	2 / 3	−0,015 / ±0,000	порог h=15 мм
СТ3	3–4 (Д-3)	2 / 3	−0,015 / ±0,000	порог h=15 мм
СТ4	5–4 (Д-4)	1 / 3	±0,000 / ±0,000	не задано
СТ5	6–4 (Д-5)	1 / 3	±0,000 / ±0,000	не задано
СТ6	7–4 (Д-7)	1 / 3	±0,000 / ±0,000	не задано

Условные обозначения

- тип 1 — инженерная доска, линии — вдоль доски
- тип 2 — керамогранит 600×600, сетка — формат плитки
- тип 3 — керамогранит 600×1200, сетка — формат плитки
- 1 — номер типа пола (экспликация полов)
- схема пола, без масштаба: плита — штриховка, стяжка — точки, звукоизоляция — зигзаг, гидроизоляция — утолщённая линия с заведением на стену
- направление укладки (длинная сторона доски)
- отметка чистого пола, м
- стык в проёме: решение не задано
- стык в проёме: порог
- СТ1 — марка стыка (ведомость стыков)
- стояк: К1 — канализация, В1 ХВС, Т3 — ГВС
- 1 — номер помещения, площадь м²

Экспликация полов

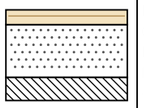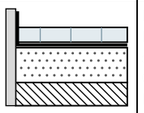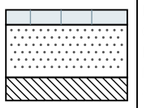Номер помещения	Тип пола	Схема пола	Данные элементов пола (наименование, толщина, основание), мм	Площадь, м²
1, 5, 6, 7	1		Инженерная доска на клею — 14 Стяжка ЦПС М200 — 50 Плита перекрытия Всего 64 мм; ЧП ±0,000, верх плиты −0,064	48,79
2, 3	2		Керамогранит на клею С2 TE S1 — 14 Гидроизоляция обмазочная, 2 слоя, с заведением на стены 200 мм — 2 Стяжка ЦПС М200 — 33 Плита перекрытия Всего 49 мм; ЧП −0,015, верх плиты −0,064	5,81
4	3		Керамогранит на клею С2 TE S1 — 14 Стяжка ЦПС М200 — 50 Плита перекрытия Всего 64 мм; ЧП ±0,000, верх плиты −0,064	13,87
			Итого	**68,47**

Раскладка покрытий

Пом.	Укладка	Старт (оси от чистовых стен), мм	Отступ 1-го ряда / крайние плитки, мм
1	вдоль стен А/В, прямая	от стены А, 1-й ряд вдоль неё	зазор от стены не задан
2	прямая, сетка 600×600, шов 2	ось X 519 от Г; ось Y 829 от А	X 518 / 518; Y 527 / 527
3	прямая, сетка 600×600, шов 2	ось X 1139 от Г; ось Y 829 от А	X 536 / 536; Y 527 / 527
4	прямая, сетка 600×1200, шов 2	ось X 1746 от Г; ось Y 2141 от А	X 541 / 541; Y 938 / 938
5	вдоль стен А/В, прямая	от стены А, 1-й ряд вдоль неё	зазор от стены не задан
6	вдоль стен А/В, прямая	от стены А, 1-й ряд вдоль неё	зазор от стены не задан
7	вдоль стен А/В, прямая	от стены А, 1-й ряд вдоль неё	зазор от стены не задан

Отметки по высоте

±0,000	чистый пол пом. 1, 4–7; отсчёт высот
−0,015	чистый пол пом. 2, 3, ниже на 15 мм
−0,064*	верх плиты — расчёт, не замер (задание на обмер)
сущ. пол	снимается до плиты; не замерен (задание на обмер)

Примечания

1. За отметку ±0,000 принят чистый пол, не существующий (блок отметок). Площади — по чистым размерам помещений, м²; размеры — в мм.
2. Стык разнотипных покрытий — по оси дверного полотна (под полотном в закрытом положении); решение стыка — по ведомости стыков.
3. Размеры помещений в свету (ширина × длина, мм), не поместившиеся на плане: пом. 2 — 1085 × 1705; пом. 4 — 3540 × 1020, 3100 × 3305, 2020 × 5; пом. 5 — 3845 × 560, 4415 × 1805, 3845 × 490, 455 × 65; пом. 7 — 3780 × 290, 5000 × 2560.
4. Пол санузлов ниже смежных помещений на 15 мм за счёт меньшей толщины стяжки (верх плиты общий — по экспликации полов); гидроизоляция по стяжке с заведением на стены не менее 200 мм (СП 29.13330.2011, п. 7.2), до облицовки — тест проливом и акт скрытых работ.
5. Выпуски канализации с уклоном и трассы водоснабжения — в слое засыпки под стяжкой (по экспликации полов); отметки, уклоны и прочистки — по листу разводки ВК 35.
6. Звукоизоляционный слой под стяжкой проектом не предусмотрен (стяжка по плите): приведённый уровень ударного шума перекрытия с полом Lnw не более 60 дБ (СП 51.13330.2011, табл. 2) подтвердить по данным дома; при превышении — плавающая стяжка по звукоизоляции с демпферной лентой по контуру и у стояков, пирог пересчитать.
7. Штучные покрытия (инженерная доска): направление — по стрелке; влажность основания по СМ не более 2,0 % (по ТУ изготовителя).
8. Ровность основания — просвет под 2-метровой рейкой не более 2 мм: пом. 1, 5, 6, 7 (инженерная доска), пом. 2, 3, 4 (керамогранит); проверить до укладки покрытия (СП 71.13330.2017, табл. 8.5).
9. Сетка на плитке — условная, в размер формата; точка старта и раскладка — по листу раскладки плитки.
10. Узор покрытия (заливка-код типа пола) прерывается под надписями — площадями помещений и отметками чистого пола.
11. Электрический тёплый пол: ТП1 — пом. 3, мат 1250×850 мм, 160 Вт; ТП2 — пом. 4, мат 1050×1850 мм, 290 Вт; контуры показаны пунктиром; датчик температуры (Д) — в гофротрубе, трасса к терморегулятору — по обмеру. Марка мата и точное положение датчика — при закупке и по обмеру.
12. Пироги полов — по экспликации полов: слои сверху вниз, толщины в мм; гидроизоляция мокрых зон — в пироге и в ведомости отделки; схема пола — без масштаба.

1000 мм · печать 1:1

Изм.	Кол.уч	Лист	№ док.	Подп.	Дата
Разраб.		Кырлан А.С.			04.11.26
Пров.					
ГИП					
Н. контр.					
Утв.					

ГД-2026-020-АИ

Квартира 68 м², элитный модерн

Общая площадь 68,47* м² · * размеры приняты, не замерены (реестр — л. 5–7, К-1)

Дизайн-проект интерьера

Стадия	Лист	Листов
РП	53	105

План полов

М 1:75

Кырлан Александр Сергеевич

выпуск 04.11.2026 № 8be4ef4c81 · стр. 60 из 117

Ведомость отделки помещений. Лист 1 из 2

Потолки, стены, низ стен, полы · площади в м², длины в м · отметки в м

Ведомость отделки помещений (форма 1 прил. А ГОСТ 21.501-2018). Лист 1 из 2

№	Наименование помещения	Потолок			Стены и перегородки			Низ стен (плинтус)			Пол		Примечание
		Вид отделки	Код цвета	S, м²	Вид отделки	Код цвета	S, м²	Вид отделки	Код цвета	L, м	Вид отделки	S, м²	
1	Кабинет 10,61 м²	ГКЛ по каркасу П113, отм. +2,590; окраска, Tikkurila Euro Power 7, глубокоматовая, 2 слоя, подготовка Q3	Tikkurila G503	10,61	Окраска, Farrow & Ball Modern Emulsion, матовая, 2 слоя, подготовка Q3 Акцент — стена B: окраска, Tikkurila Euro Power 7, колеровка по NCS, матовая, 2 слоя, подготовка Q3	Farrow & Ball No. 2003 Farrow & Ball No. 30	20,12 9,60	Плинтус МДФ h=80 мм, аналог: МДФ под покраску 80×16	Farrow & Ball No. 2003	12,3	Аналог: инженерная доска, дуб натуральный, масло, 1-полосная, 14/4 мм, на клею; тип 1, отм. ЧП ±0,000	10,61	Н стен 2590 (до потолка); плинтус в цвет: стены
2	Санузел 1,85 м²	ГКЛВ по каркасу П113, отм. +2,505; окраска, Tikkurila Euro Power 7, матовая, 2 слоя, подготовка Q3	Tikkurila G503	1,85	Облицовка плиткой, аналог: керамогранит под травертин, матовый, 600×1200×9 мм, клей C2 TE S1, затирка CG2WA	по артикулу	11,76	нет			Аналог: керамогранит ректифицированный под травертин, матовый, 600×600×9 мм; тип 2, отм. ЧП −0,015	1,85	Н стен 2520 (до потолка); тёплый пол; гидроизоляция обмазочная, 2 слоя, с заведением на стены 200 мм (по пирогу пола); тест проливом и акт скрытых работ
3	Ванная 3,96 м²	ГКЛВ по каркасу П113, отм. +2,505; окраска, Tikkurila Euro Power 7, матовая, 2 слоя, подготовка Q3	Tikkurila G503	3,96	Облицовка плиткой, аналог: керамогранит под травертин, матовый, 600×1200×9 мм, клей C2 TE S1, затирка CG2WA	по артикулу	17,72	нет			Аналог: керамогранит ректифицированный под травертин, матовый, 600×600×9 мм; тип 2, отм. ЧП −0,015	3,96	Н стен 2520 (до потолка); тёплый пол; гидроизоляция обмазочная, 2 слоя, с заведением на стены 200 мм; над ванной — до 2000 и 300 мм за борт (по пирогу пола); тест проливом и акт скрытых работ
4	Прихожая 13,87 м²	ГКЛ/Существующий потолок по каркасу П113, отм. +2,550; +2,650; окраска, Tikkurila Euro Power 7, глубокоматовая, 2 слоя, подготовка Q3	Tikkurila G503	13,87	Окраска, Farrow & Ball Modern Emulsion, матовая, 2 слоя, подготовка Q3	Farrow & Ball No. 2003	27,58	Плинтус МДФ h=80 мм, аналог: МДФ под покраску 80×16	Farrow & Ball No. 2003	9,8	Аналог: керамогранит ректифицированный под травертин, матовый, 600×1200×9 мм; тип 3, отм. ЧП ±0,000	13,87	Н стен 2550 (до потолка); тёплый пол; матовая моющаяся, класс 1 EN 13300 — осознанно вместо полуматовой; плинтус в цвет: стены
5	Кухня-столовая 12,04 м²	ГКЛ по каркасу П113, отм. +2,590; окраска, Tikkurila Euro Power 7, глубокоматовая, 2 слоя, подготовка Q3	Tikkurila G503	12,04	Окраска, Farrow & Ball Modern Emulsion, матовая, 2 слоя, подготовка Q3 Акцент — стена B: окраска, Tikkurila Euro Power 7, колеровка по NCS, матовая, 2 слоя, подготовка Q3 Фартук кухни (стена A): облицовка керамогранитом, аналог: керамогранит под травертин, матовый, 1200×600×9 мм, клей C2 TE S1, затирка CG2WA	Farrow & Ball No. 2003 Farrow & Ball No. 281 по артикулу	22,56 9,96 1,68	Плинтус МДФ h=80 мм, аналог: МДФ под покраску 80×16	Farrow & Ball No. 2003	13,8	Аналог: инженерная доска, дуб натуральный, масло, 1-полосная, 14/4 мм, на клею; тип 1, отм. ЧП ±0,000	12,04	Н стен 2590 (до потолка); матовая моющаяся, класс 1 EN 13300 — осознанно вместо полуматовой; плинтус в цвет: стены
6	Гостиная 12,24 м²	ГКЛ по каркасу П113, отм. +2,590; окраска, Tikkurila Euro Power 7, глубокоматовая, 2 слоя, подготовка Q3	Tikkurila G503	12,24	Окраска, Farrow & Ball Modern Emulsion, матовая, 2 слоя, подготовка Q3 Акцент — стена A: окраска, Farrow & Ball Modern Emulsion, матовая, 2 слоя, подготовка Q3	Farrow & Ball No. 2003 Farrow & Ball No. 43	22,36 9,92	Плинтус МДФ h=80 мм, аналог: МДФ под покраску 80×16	Farrow & Ball No. 2003	13,3	Аналог: инженерная доска, дуб натуральный, масло, 1-полосная, 14/4 мм, на клею; тип 1, отм. ЧП ±0,000	12,24	Н стен 2590 (до потолка); плинтус в цвет: стены
7	Спальня 13,90 м²	ГКЛ по каркасу П113, отм. +2,590; окраска, Tikkurila Euro Power 7, глубокоматовая, 2 слоя, подготовка Q3	Tikkurila G503	13,90	Окраска, Farrow & Ball Modern Emulsion, матовая, 2 слоя, подготовка Q3 Акцент — стена B: окраска, Farrow & Ball Modern Emulsion, матовая, 2 слоя, подготовка Q3	Farrow & Ball No. 2003 Farrow & Ball No. 34	23,37 12,95	Плинтус МДФ h=80 мм, аналог: МДФ под покраску 80×16	Farrow & Ball No. 2003	14,8	Аналог: инженерная доска, дуб натуральный, масло, 1-полосная, 14/4 мм, на клею; тип 1, отм. ЧП ±0,000	13,90	Н стен 2590 (до потолка); плинтус в цвет: стены

Примечания

1. Ведомость продолжена на листе 2 из 2; итоги, сводка площадей и примечания — на последнем листе ведомости.

Допущения и предложения на листе

Основа листа: планировка по обводу плана заказчика, не замерена (К-1); высота до плиты 2650 мм от чистого пола — решение автора (ИЗ-1); отметки плана потолков сдвинуты на -95 мм (+2.745 плана = низ плиты), не замерено (К-2); толщины стен приняты: наружные 260 мм, перегородки 130 мм (К-1); положение стен и проёмов — по брифу без обмера и плана БТИ (К-1); разрешённая мощность 10 кВт принята, ТУ не переданы (К-6); вентканалы приняты, в брифе не заданы (К-5); тип дома, перекрытие и несущие стены не известны — документов нет (К-3); плита электрическая — принята, в брифе не указано (К-6); система заземления TN-C-S принята, ТУ не переданы (К-6); число жильцов 2 принято, в брифе не указано (К-9); подрайон климата не задан — принят не северный (жилые от 2,5 м) (К-26).

Знак «**» — предложение проектировщика, заказчиком не утверждено (согласовать с заказчиком): К-7: акцент пом. 1, 5–7; К-8: пол пом. 1, 4–7, плинтус пом. 1, 4–7, стены пом. 2, 3, фартук пом. 5 — артикул изделия не выбран: позиция описана характеристиками («аналог по характеристикам»), артикул выбирается при закупке; пол пом. 2, 3 — пирог пола: стяжка 33 мм и обмазочная гидроизоляция добавлены разработчиком проекта; артикул изделия не выбран: позиция описана характеристиками («аналог по характеристикам»), артикул выбирается при закупке.

См. лист открытых вопросов (лист 5, записи К-1, К-3, К-5–К-9; лист 6, запись К-26).

Изм.	Кол.уч	Лист	№ док.	Подп.	Дата
Разраб.		Кырлан А.С.			04.11.26
Пров.					
ГИП					
Н. контр.					
Утв.					

ГД-2026-020-АИ

Квартира 68 м², элитный модерн

Общая площадь 68,47* м² · * размеры приняты, не замерены (реестр — л. 5–7, К-1)

Дизайн-проект интерьера	Стадия	Лист	Листов
	РП	54	105

Ведомость отделки помещений. Лист 1 из 2

М б/м

Кырлан Александр Сергеевич

выпуск 04.11.2026 № 8be4ef4c81 · стр. 61 из 117

Ведомость отделки помещений. Лист 2 из 2

Потолки, стены, низ стен, полы · площади в м², длины в м · отметки в м

Ведомость отделки помещений (форма 1 прил. А ГОСТ 21.501-2018). Лист 2 из 2

№	Наименование помещения	Потолок			Стены и перегородки			Низ стен (плинтус)			Пол		Примечание
		Вид отделки	Код цвета	S, м²	Вид отделки	Код цвета	S, м²	Вид отделки	Код цвета	L, м	Вид отделки	S, м²	
	Итого			**68,47**			**189,56**			**63,9**		**68,47**	

Сводка площадей по материалам отделки

Поверхность	Материал / код цвета	Серия	Площадь, м²
Потолок	Tikkurila G503	Euro Power 7	68,47
Стены	Farrow & Ball No. 2003	Modern Emulsion	115,98
Стены	Farrow & Ball No. 30	Euro Power 7, колеровка по NCS	9,60
Стены	облицовка плиткой 600×1200×9 мм	аналог: керамогранит под травертин, матовый	29,47
Стены	Farrow & Ball No. 281	Euro Power 7, колеровка по NCS	9,96
Стены	Farrow & Ball No. 43	Modern Emulsion	9,92
Стены	Farrow & Ball No. 34	Modern Emulsion	12,95
Фартук	облицовка керамогранитом 1200×600×9 мм	аналог: керамогранит под травертин, матовый	1,68

Допущения и предложения на листе

Основа листа: планировка по обводу плана заказчика, не замерена (К-1); высота до плиты 2650 мм от чистого пола — решение автора (ИЗ-1); отметки плана потолков сдвинуты на -95 мм (+2.745 плана = низ плиты), не замерено (К-2); толщины стен приняты: наружные 260 мм, перегородки 130 мм (К-1); положение стен и проёмов — по брифу без обмера и плана БТИ (К-1); разрешённая мощность 10 кВт принята, ТУ не переданы (К-6); вентканалы приняты, в брифе не заданы (К-5); тип дома, перекрытие и несущие стены не известны — документов нет (К-3); плита электрическая — принята, в брифе не указано (К-6); система заземления TN-C-S принята, ТУ не переданы (К-6); число жильцов 2 принято, в брифе не указано (К-9); подрайон климата не задан — принят не северный (жилые от 2,5 м) (К-26).

Знак «**» — предложение проектировщика, заказчиком не утверждено (согласовать с заказчиком): К-7: акцент пом. 1, 5–7; К-8: пол пом. 1, 4–7, плинтус пом. 1, 4–7, стены пом. 2, 3, фартук пом. 5 — артикул изделия не выбран: позиция описана характеристиками («аналог по характеристикам»), артикул выбирается при закупке; пол пом. 2, 3 — пирог пола: стяжка 33 мм и обмазочная гидроизоляция добавлены разработчиком проекта; артикул изделия не выбран: позиция описана характеристиками («аналог по характеристикам»), артикул выбирается при закупке.

См. лист открытых вопросов (лист 5, записи К-1, К-3, К-5–К-9; лист 6, запись К-26).

Примечания

1. Площади поверхностей — по чистым граням стен до отделки: стены = периметр × высоту от чистого пола помещения до низа потолка минус проёмы (облицовка плиткой — до верха облицовки); плинтус = периметр минус дверные проёмы; пол и потолок — по площади помещения. Количество плиток по раскладке. Площади помещений — с учётом всех частей помещения; откосы в площадь стен не входят.
2. Акцентные стены и фартук — отдельными строками, их площадь вычтена из основной отделки стен помещения; фартук — над нижними модулями кухни от столешницы до низа навесных шкафов, где шкафов нет — на 600 мм.
3. Плинтус — длина по периметру за вычетом дверных проёмов; примыкания к наличникам и встроенной мебели — по развёрткам.
4. Формат плитки — Ш×В×Т (ширина × высота в положении укладки × толщина), мм; на полу — вдоль стен А/В × вдоль стен Б/Г.
5. Коды цвета — по веерам производителей; колеровка каждой краски одной партией, проверка выкраса при свете D65 и при лампах проекта.
6. Уровни подготовки Q1–Q4 — система Knauf, не норма ГОСТ/СП; допуски поверхностей — по СП 71.13330.2017 (действующая редакция).
7. «аналог:» — изделие задано характеристиками, марку и артикул согласовать с заказчиком до закупки.

Изм.	Кол.уч	Лист	№ док.	Подп.	Дата	ГД-2026-020-АИ		
						Квартира 68 м², элитный модерн		
						Общая площадь 68,47* м² · * размеры приняты, не замерены (реестр — л. 5–7, К-1)		
Разраб.		Кырлан А.С.			04.11.26	Дизайн-проект интерьера	Стадия	Лист	Листов
Пров.							РП	55	105
ГИП									
Н. контр.						Ведомость отделки помещений. Лист 2 из 2	Кырлан Александр Сергеевич		
Утв.						М б/м			

Колерная карта

Цвета и материалы по помещениям · палитра проекта · выкрасы на согласование

ПРЕДВАРИТЕЛЬНО · не для производства работ · открыто пунктов: 25 (реестр — л. 5–7)

Колерная карта по помещениям

Помещение	Поверхность	Образец	Поз.	Система и код цвета	Производитель, линейка / материал, артикул	Блеск	Класс истирания	LRV	Площадь
1. Кабинет 10,61 м²	стены		**К1**	Farrow & Ball No. 2003	Farrow & Ball · Modern Emulsion	матовая	1	86	20,1 м²
	акцент В		**К2**	Farrow & Ball No. 30	Tikkurila · Euro Power 7, колеровка по NCS	матовая	1	7	9,6 м²
	потолок		**К3**	Tikkurila G503	Tikkurila · Euro Power 7	глубокомат.	2	89	10,6 м²
	пол		**КМ1**	по образцу	инженерная доска · аналог по хар.				10,6 м²
	плинтус		**К4**	Farrow & Ball No. 2003	МДФ · в цвет Farrow & Ball			86	12,3 м
2. Санузел 1,85 м²	стены		**КМ2**	по образцу	плитка · аналог по хар.				11,8 м²
	потолок		**К5**	Tikkurila G503	Tikkurila · Euro Power 7	матовая	1	89	1,9 м²
	пол		**КМ3**	по образцу	керамогранит · аналог по хар.				1,9 м²
3. Ванная 3,96 м²	стены		**КМ2**	по образцу	плитка · аналог по хар.				17,7 м²
	потолок		**К5**	Tikkurila G503	Tikkurila · Euro Power 7	матовая	1	89	4,0 м²
	пол		**КМ3**	по образцу	керамогранит · аналог по хар.				4,0 м²
4. Прихожая 13,87 м²	стены		**К1**	Farrow & Ball No. 2003	Farrow & Ball · Modern Emulsion	матовая	1	86	27,6 м²
	потолок		**К3**	Tikkurila G503	Tikkurila · Euro Power 7	глубокомат.	2	89	13,9 м²
	пол		**КМ4**	по образцу	керамогранит · аналог по хар.				13,9 м²
	плинтус		**К4**	Farrow & Ball No. 2003	МДФ · в цвет Farrow & Ball			86	9,8 м
5. Кухня-столовая 12,04 м²	стены		**К1**	Farrow & Ball No. 2003	Farrow & Ball · Modern Emulsion	матовая	1	86	22,6 м²
	акцент В		**К6**	Farrow & Ball No. 281	Tikkurila · Euro Power 7, колеровка по NCS	матовая	1	10.1	10,0 м²
	потолок		**К3**	Tikkurila G503	Tikkurila · Euro Power 7	глубокомат.	2	89	12,0 м²
	пол		**КМ1**	по образцу	инженерная доска · аналог по хар.				12,0 м²
	плинтус		**К4**	Farrow & Ball No. 2003	МДФ · в цвет Farrow & Ball			86	13,8 м
	фартук		**КМ5**	по образцу	керамогранит · аналог по хар.				1,7 м²
6. Гостиная 12,24 м²	стены		**К1**	Farrow & Ball No. 2003	Farrow & Ball · Modern Emulsion	матовая	1	86	22,4 м²
	акцент А		**К7**	Farrow & Ball No. 43	Farrow & Ball · Modern Emulsion	матовая	1	11.8	9,9 м²
	потолок		**К3**	Tikkurila G503	Tikkurila · Euro Power 7	глубокомат.	2	89	12,2 м²
	пол		**КМ1**	по образцу	инженерная доска · аналог по хар.				12,2 м²
	плинтус		**К4**	Farrow & Ball No. 2003	МДФ · в цвет Farrow & Ball			86	13,3 м
7. Спальня 13,9 м²	стены		**К1**	Farrow & Ball No. 2003	Farrow & Ball · Modern Emulsion	матовая	1	86	23,4 м²
	акцент В		**К8**	Farrow & Ball No. 34	Farrow & Ball · Modern Emulsion	матовая	1	22	12,9 м²
	потолок		**К3**	Tikkurila G503	Tikkurila · Euro Power 7	глубокомат.	2	89	13,9 м²
	пол		**КМ1**	по образцу	инженерная доска · аналог по хар.				13,9 м²
	плинтус		**К4**	Farrow & Ball No. 2003	МДФ · в цвет Farrow & Ball			86	14,8 м

Перечень выкрасов на согласование

№	Код	Бренд / веер	Пом. / стена	Подложка	Формат	Статус
1	No. 2003	Farrow & Ball	1, 4, 5, 6, 7	ГКЛ с грунтом; МДФ под эмаль	600×1000; 300×600	к выполнению
2	No. 30	Farrow & Ball	1 В	ГКЛ с грунтом	600×1000	к выполнению
3	G503	Tikkurila	1, 2, 3, 4, 5, 6, 7	ГКЛ с грунтом	600×1000	к выполнению
4	No. 281	Farrow & Ball	5 В	ГКЛ с грунтом	600×1000	к выполнению
5	No. 43	Farrow & Ball	6 А	ГКЛ с грунтом	600×1000	к выполнению
6	No. 34	Farrow & Ball	7 В	ГКЛ с грунтом	600×1000	к выполнению

Примечания

1. Цвет на листе и на экране — ориентир. До покраски — выкрас на объекте: не меньше А3 (или лист ГКЛ), на грунте под эту краску, не на белой шпаклёвке, в 2 слоя; на обороте — код, бренд, веер, дата. Смотреть днём и вечером, рядом с образцами пола и плитки; к основному цвету стен — ещё 2 соседних оттенка. Красить только в цвет утверждённого выкраса.
2. Краску заказывать по коду из графы «Система и код цвета» у бренда этого кода, не «аналогом» другого; весь объём одного кода — одной партией, колеруемую краску — за один проход машины.
3. Площади — те же, что в ведомости отделки (лист 54); сколько краски заказать — в спецификации отделочных материалов (лист 57).

Допущения и предложения на листе. Основа листа: планировка по обводу плана заказчика, не замерена (К-1); высота до плиты 2650 мм от чистого пола — решение автора (ИЗ-1); отметки плана потолков сдвинуты на -95 мм (+2.745 плана = низ плиты), не замерено (К-2); толщины стен приняты: наружные 260 мм, перегородки 130 мм (К-1); положение стен и проёмов — по брифу без обмера и плана БТИ (К-1); разрешённая мощность 10 кВт принята, ТУ не переданы (К-6); вентканалы приняты, в брифе не заданы (К-5); тип дома, перекрытие и несущие стены не известны — документов нет (К-3); плита электрическая — принята, в брифе не указано (К-6); система заземления TN-C-S принята, ТУ не переданы (К-6); число жильцов 2 принято, в брифе не указано (К-9); подрайон климата не задан — принят не северный (жилые от 2,5 м) (К-26). Знак «**» — предложение проектировщика, заказчиком не утверждено (согласовать с заказчиком): К-7: акцент пом. 1, 5–7; К-8: пол пом. 1, 4–7, плинтус пом. 1, 4–7, стены пом. 2, 3, фартук пом. 5 — артикул изделия не выбран: позиция описана характеристиками («аналог по характеристикам»), артикул выбирается при закупке; пол пом. 2, 3 — пирог пола: стяжка 33 мм и обмазочная гидроизоляция добавлены разработчиком проекта; артикул изделия не выбран: позиция описана характеристиками («аналог по характеристикам»), артикул выбирается при закупке. См. лист открытых вопросов (лист 5, записи К-1, К-3, К-5–К-9; лист 6, записи К-21, К-26); по листу — К-7, К-21.

Схема квартиры: цвет стен и акценты (б/м)

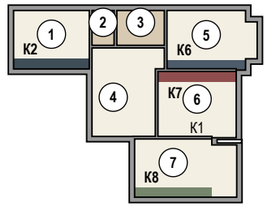


Схема палитры проекта


Стиль: Современный (контемпорари) 60% + Тихая роскошь (quiet luxury) 40% · схема: комплементарная

основной	основной	основной	второстепенный	второстепенный	второстепенный	акцентный	акцентный	акцентный	акцентный	акцентный	акцентный	акцентный	акцентный
Tikkurila G503	Farrow & Ball No. 2003	Tikkurila V503	Farrow & Ball No. 239	NCS S 2010-Y30R	Tikkurila H497	NCS S 7010-Y50R	NCS S 6020-G70Y	Farrow & Ball No. 228	Farrow & Ball No. 43	Farrow & Ball No. 39	Farrow & Ball No. 281	Farrow & Ball No. 43	Farrow & Ball No. 34
Calla LRV 89 потолок 1,2,3,4,5,6,7; текстиль/декор 1,6,7	Pointing LRV 86 стены 1,4,5,6,7; плинтус 1,4,5,6,7	Winter LRV 86 в отделке не применён	Shaded White LRV 63 текстиль/декор 1,5,6,7	светлый кэмел LRV 60 текстиль/декор 6,7	Pumice LRV 57 в отделке не применён	кофе / табак LRV 8 в отделке не применён	олива LRV 12 в отделке не применён	Bancha LRV 14 текстиль/декор 6	Mouse's Back LRV 26 текстиль/декор 7	Hague Blue — глубокий сине-зелёный LRV 7 акцент 1	Stiffkey Blue — чернильный синий LRV 10.1 акцент 5	Eating Room Red — брусничный красный LRV 11.8 акцент 6	Calke Green — традиционный шалфей LRV 22 акцент 7

План 60/30/10



Окраска, факт — по площади стен, акцентов, потолков

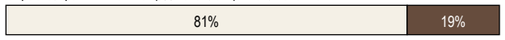

окрашено всего 226,9 м²; второстепенный тон несут мебель и текстиль

Условные обозначения

- **К1** Farrow & Ball No. 2003 · Pointing · Modern Emulsion · матовая · кл. 1
- **К2** Farrow & Ball No. 30 · Hague Blue — глубокий сине-зелёный · Euro Power 7, колеровка по NCS · матовая · кл. 1
- **К3** Tikkurila G503 · Calla · Euro Power 7 · глубокомат. · кл. 2
- **К4** Farrow & Ball No. 2003 · Pointing · МДФ
- **К5** Tikkurila G503 · Calla · Euro Power 7 · матовая · кл. 1
- **К6** Farrow & Ball No. 281 · Stiffkey Blue — чернильный синий · Euro Power 7, колеровка по NCS · матовая · кл. 1
- **К7** Farrow & Ball No. 43 · Eating Room Red — брусничный красный · Modern Emulsion · матовая · кл. 1
- **К8** Farrow & Ball No. 34 · Calke Green — традиционный шалфей · Modern Emulsion · матовая · кл. 1
- дерево (доска, паркет, ламинат) — рисунок досок
- керамогранит, плитка, камень — сетка швов по формату
- **КМ1** аналог: инженерная доска, дуб натуральный, масло, 1-полосная, 14/4 мм
- **КМ2** плитка · аналог: керамогранит под травертин, матовый, 600×1200×9 мм
- **КМ3** аналог: керамогранит ректифицированный под травертин, матовый, 600×600×9 мм
- **КМ4** аналог: керамогранит ректифицированный под травертин, матовый, 600×1200×9 мм
- **КМ5** аналог: керамогранит под травертин, матовый, 1200×600×9 мм

К — краска, КМ — отделочный материал (тон КМ — по описанию, эталон — образец материала); кл. — класс истирания (1 — самый стойкий к мытью); LRV — светлота цвета: 0 — чёрный, 100 — белый

Изм.	Кол.уч	Лист	№ док.	Подп.	Дата
Разраб.		Кырлан А.С.			04.11.26
Пров.					
ГИП					
Н. контр.					
Утв.					

ГД-2026-020-АИ

Квартира 68 м², элитный модерн

Общая площадь 68,47* м² · * размеры приняты, не замерены (реестр — л. 5–7, К-1)

Дизайн-проект интерьера

Стадия	Лист	Листов
РП	56	105

Колерная карта

М б/м

Кырлан Александр Сергеевич

выпуск 04.11.2026 № 8be4ef4c81 · стр. 63 из 117

Спецификация отделочных материалов

ПРЕДВАРИТЕЛЬНО · не для производства работ · открыто пунктов: 25 (реестр — л. 5–7)

Форма 1 по ГОСТ 21.110-2013 · количества — из геометрии проекта, с запасом

Поз.	Наименование и техническая характеристика	Тип, марка, обозначение документа	Код продукции	Поставщик	Ед. изм.	Кол.	Масса 1 ед., кг	Примечание
	Лакокрасочные материалы							
1	Краска интерьерная водно-дисперсионная акриловая для стен, матовая, класс мокрого истирания 1 по EN 13300, база A; цвет по вееру Farrow & Ball No. 2003 «Pointing», колеровка машинная	Farrow & Ball Modern Emulsion		Farrow & Ball	л	32,5		поз. К1 колерной карты; пом. 1, 4, 5, 6, 7; S = 116,0 м² × 2 сл. × 0,12 л/м² = 27,8 л, +10 % и 0,5 л на подкраску → ≥ 31,1 л; тара 6 × 5 л + 1 × 2,5 л
2	Краска интерьерная водно-дисперсионная акриловая для акцентных стен, матовая, класс мокрого истирания 1 по EN 13300, база C; цвет по вееру Farrow & Ball No. 30 «Hague Blue — глубокий сине-зелёный», колеровка машинная	Tikkurila Euro Power 7, колеровка по NCS		Tikkurila	л	5		поз. К2 колерной карты; пом. 1; S = 9,6 м² × 2 сл. × 0,12 л/м² = 2,3 л, +10 % и 0,5 л на подкраску → ≥ 3,0 л; тара 1 × 5 л
3	Краска интерьерная водно-дисперсионная акриловая для потолков, глубокоматовая, класс мокрого истирания 2 по EN 13300, база A; цвет по вееру Tikkurila G503 «Calla», колеровка машинная	Tikkurila Euro Power 7		Tikkurila	л	17,1		поз. К3 колерной карты; пом. 1, 4, 5, 6, 7; S = 62,7 м² × 2 сл. × 0,12 л/м² = 15,0 л, +10 % и 0,5 л на подкраску → ≥ 17,0 л; тара 1 × 9 л + 3 × 2,7 л
4	Краска интерьерная водно-дисперсионная акриловая для потолков, матовая, класс мокрого истирания 1 по EN 13300, база A; цвет по вееру Tikkurila G503 «Calla», колеровка машинная	Tikkurila Euro Power 7		Tikkurila	л	2,7		поз. К5 колерной карты; пом. 2, 3; S = 5,8 м² × 2 сл. × 0,12 л/м² = 1,4 л, +10 % и 0,5 л на подкраску → ≥ 2,0 л; тара 1 × 2,7 л
5	Краска интерьерная водно-дисперсионная акриловая для акцентных стен, матовая, класс мокрого истирания 1 по EN 13300, база C; цвет по вееру Farrow & Ball No. 281 «Stiffkey Blue — чернильный синий», колеровка машинная	Tikkurila Euro Power 7, колеровка по NCS		Tikkurila	л	5		поз. К6 колерной карты; пом. 5; S = 10,0 м² × 2 сл. × 0,12 л/м² = 2,4 л, +10 % и 0,5 л на подкраску → ≥ 3,1 л; тара 1 × 5 л
6	Краска интерьерная водно-дисперсионная акриловая для акцентных стен, матовая, класс мокрого истирания 1 по EN 13300, база C; цвет по вееру Farrow & Ball No. 43 «Eating Room Red — брусничный красный», колеровка машинная	Farrow & Ball Modern Emulsion		Farrow & Ball	л	5		поз. К7 колерной карты; пом. 6; S = 9,9 м² × 2 сл. × 0,12 л/м² = 2,4 л, +10 % и 0,5 л на подкраску → ≥ 3,1 л; тара 1 × 5 л
7	Краска интерьерная водно-дисперсионная акриловая для акцентных стен, матовая, класс мокрого истирания 1 по EN 13300, база C; цвет по вееру Farrow & Ball No. 34 «Calke Green — традиционный шалфей», колеровка машинная	Farrow & Ball Modern Emulsion		Farrow & Ball	л	5		поз. К8 колерной карты; пом. 7; S = 12,9 м² × 2 сл. × 0,12 л/м² = 3,1 л, +10 % и 0,5 л на подкраску → ≥ 3,9 л; тара 1 × 5 л
8	Краска для МДФ и дерева в цвет Farrow & Ball No. 2003 «Pointing» — окраска плинтуса; блеск не ниже блеска стен	марка не задана			л	1,7		поз. К4; пом. 1, 4, 5, 6, 7; L = 63,9 м, S = 6,1 м² × 2 сл. × 0,12 л/м² + 10 %; продукт подобрать в веере Farrow & Ball
9	Грунтовка акриловая под окраску стен и потолков — из системы производителя краски	по системе краски			м²	227		площадь окраски стен, акцентов и потолков; 1 слой перед окраской; расход — по ТУ грунтовки
	Плитка и керамогранит							
10	Керамогранит под травертин, 600×600×9 мм, ректификат, водопоглощение 0,1 % (BIa), противоскольжение R10, PEI IV	аналог по характеристикам			м²	7,56		шов 2 мм; Санузел, пол; Ванная, пол; по раскладке 18 шт (S = 5,81 м²), с запасом 21 шт
11	Керамогранит под травертин, 600×1200×9 мм, ректификат, водопоглощение 0,1 %	аналог по характеристикам			м²	43,92		шов 2 мм; Санузел, стены А–Г; Санузел, короб инсталляции; Ванная, стены А–Г; по раскладке 52 шт (S = 30,23 м²), с запасом 61 шт
12	Керамогранит ректифицированный под травертин, матовый, 600×1200×9 мм, водопоглощение 0,1 % (BIa), противоскольжение R10, PEI IV	аналог по характеристикам			м²	19,44		шов 2 мм; Прихожая, пол; по раскладке 24 шт (S = 13,87 м²), с запасом 27 шт
13	Керамогранит под травертин, матовый, 1200×600×9 мм, ректификат, водопоглощение 0,1 % (BIa)	аналог по характеристикам			м²	4,32		шов 2 мм; Кухня-столовая, фартук (ст. А); по раскладке 5 шт (S = 1,68 м²), с запасом 6 шт
	Напольные покрытия							
14	Инженерная доска, дуб натуральный, масло, 1-полосная, 14/4 мм, эмиссия E1, укладка на клей	аналог по характеристикам			м²	52,3		пом. 1, 5, 6, 7; S = 48,79 м² + 7 % (прямая укладка); к заказу — кратно упаковке
15	Клей для паркета и инженерной доски, эластичный (СМП / полиуретановый)	по рекомендации производителя доски			м²	49		площадь приклейки; расход и шпатель — по ТУ клея
	Погонажные изделия							
16	Плинтус МДФ под покраску 80×16, крепление к стене, окраска в цвет Farrow & Ball No. 2003	аналог по характеристикам			м	71		пом. 1, 4, 5, 6, 7; L = 63,9 м (периметр без дверных проёмов) + 10 % на подрезку; в штуках — по длине планки
	Смеси и материалы для облицовки							
17	Затирка для швов плитки, класс CG2WA по EN 13888	Mapei Ultracolor Plus 132		Mapei	кг	4,1		по раскладке (a+b)/(a·b) × шов × t × 1,6 + 10 %; в т. ч. 0,1 кг — позиции раскладки без марки
18	Клей плиточный C2 TE S1 по EN 12004, слой 5 мм	Ceresit CM 17		Ceresit	кг	411		17 меш. по 25 кг; 1,5 кг/м² на 1 мм слоя + 10 %; в т. ч. 14 кг — позиции раскладки без марки
19	Гидроизоляция обмазочная мокрых зон: пол, стены по периметру, зоны замачивания; 2 слоя с армирующей лентой в углах	аналог по характеристикам			м²	15,8		площадь по листу раскладки плитки + 10 %; расход смеси — по ТУ
20	Лента демпферная по периметру пола из плитки	аналог по характеристикам			м	26,9		периметр без дверных проёмов + 10 %

Примечания

1. Количества — из геометрии проекта: площади поверхностей по чистым граням стен до отделки (те же, что в ведомости отделки и колерной карте), плитка, клей и затирка — по раскладке плиточника; в графе «Кол.» — к заказу, с запасом.
2. Краска: расход 0,12 л/м² на слой в 2 слоя, если по ТУ не задан иной; запас 10 % и 0,5 л на подкраску каждого кода. Один код — одна партия, колеровка машинная в колеровочном центре бренда; в заказ — только после утверждения выкраса (колерная карта). Фасовка — по каталогу бренда на дату выпуска; к заказу — не меньше расчётного объёма.
3. «Аналог по характеристикам» — допускается изделие другого производителя с характеристиками не ниже указанных, по согласованию с автором проекта.
4. Графы «Код продукции» и «Масса 1 ед.» не заполнены: коды по классификатору продукции не присвоены, масса единицы до 25 кг (ГОСТ 21.110-2013).
5. Грунтовка и клей для доски указаны площадью обработки; объём — по ТУ выбранного продукта.

Допущения и предложения на листе. Основа листа: планировка по обводу плана заказчика, не замерена (К-1); высота до плиты 2650 мм от чистого пола — решение автора (ИЗ-1); отметки плана потолков сдвинуты на -95 мм (+2.745 плана = низ плиты), не замерено (К-2); толщины стен приняты: наружные 260 мм, перегородки 130 мм (К-1); положение стен и проёмов — по брифу без обмера и плана БТИ (К-1); разрешённая мощность 10 кВт принята, ТУ не переданы (К-6); вентканалы приняты, в брифе не заданы (К-5); тип дома, перекрытие и несущие стены не известны — документов нет (К-3); плита электрическая — принята, в брифе не указано (К-6); система заземления TN-C-S принята, ТУ не переданы (К-6); число жильцов 2 принято, в брифе не указано (К-9); подрайон климата не задан — принят не северный (жилые от 2,5 м) (К-26). Знак «**» — предложено, не утверждено (согласовать): К-7: акцент пом. 1, 5–7; К-8: пол пом. 1–7, плинтус пом. 1, 4–7, стены пом. 2, 3, фартук пом. 5. См. лист открытых вопросов (лист 5, записи К-1, К-3, К-5–К-9; лист 6, запись К-26).

Изм.	Кол.уч	Лист	№ док.	Подп.	Дата
Разраб.		Кырлан А.С.			04.11.26
Пров.					
ГИП					
Н. контр.					
Утв.					

ГД-2026-020-АИ

Квартира 68 м², элитный модерн

Общая площадь 68,47* м² · * размеры приняты, не замерены (реестр — л. 5–7, К-1)

Дизайн-проект интерьера

Стадия	Лист	Листов
РП	57	105

Спецификация отделочных материалов


М б/м

Кырлан Александр Сергеевич

Концепция декора и визуализации


Современный (контемпорари) · элитный модерн (quiet luxury) · визуализации, палитра, материалы, ключевые предметы

ПРЕДВАРИТЕЛЬНО · не для производства работ · открыто пунктов: 25 (реестр — л. 5–7)

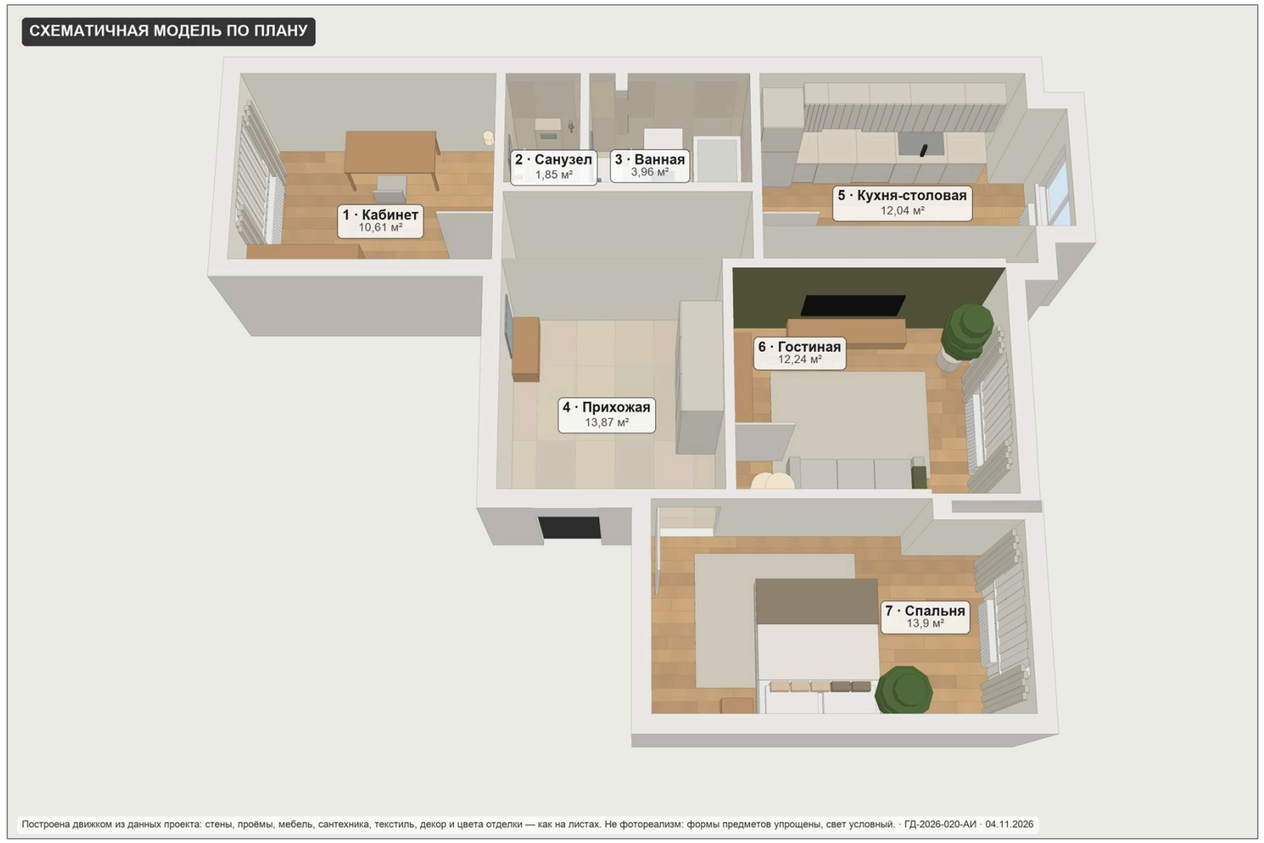

Визуализация 1. Вид сверху (3D), схематичная модель по плану: мебель, текстиль и декор из данных проекта

Расстановка — по плану мебели (лист 19); шторы, ковры, картины и растения — по плану текстиля и декора (лист 59).

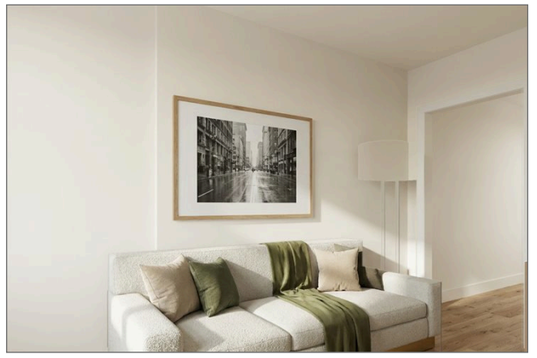


Визуализация 8. Гостиная (пом. 6)

шторы Т4**, Т5** · ковёр Т6** · картины ДК4**, ДК5** · растение ДК6 · подушки, пледы Т7**, Т8**, Т9**



Визуализация 6. Кухня-столовая (пом. 5)

шторы Т3

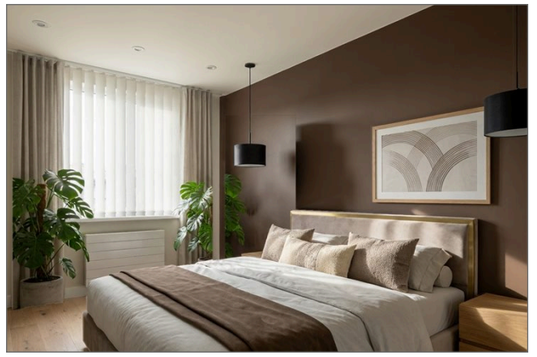

Визуализация 4. Спальня (пом. 7)

шторы Т10**, Т11** · ковёр Т12** · картина ДК7** · растение ДК8 · подушки, пледы Т13**, Т14**, Т15**



Визуализация 10. Кабинет (пом. 1)

шторы Т1**, Т2**

Палитра 60/30/10 и цвета текстиля

60 % 30 % 10 %

- Tikkurila G503 (Calla), LRV 89 — 60 % база — Т2, Т5, Т11
- Tikkurila V503 (Winter), LRV 86 — 60 % база
- NCS S 2010-Y30R (светлый кэмел), LRV 60 — 30 % второй цвет — Т7, Т13
- NCS S 7010-Y50R (кофе / табак), LRV 8 — 10 % акцент
- Farrow & Ball No. 298 (Bancha), LRV 14 — 10 % акцент — Т8, Т9
- Farrow & Ball No. 2003 (Pointing), LRV 86 — 60 % база
- Farrow & Ball No. 201 (Shaded White), LRV 63 — 30 % второй цвет — Т1, Т3, Т4, Т6, Т10, Т12
- Tikkurila H487 (Pumice), LRV 57 — 30 % второй цвет
- NCS S 6020-G70Y (олива), LRV 12 — 10 % акцент
- Farrow & Ball No. 40 (Mouse's Back), LRV 26 — 10 % акцент — Т14, Т15

Материалы и фактуры



Дуб натуральный

пол: пом. 1, 5, 6, 7; рамы ДК4**, ДК5**, ДК7**



Травертин (керамогранит)

пол и стены санузлов, фартук: пом. 2, 3, 4, 5



Букле

подушки: Т13**



Лён

рулонная, подушки: Т3, Т7**, Т14**



Бронза и чёрный металл

фурнитура, светильники — бронза

Ключевые предметы

— Диван М20** 2000×950 — гостиная; подушки и плед Т7**, Т8**, Т9**
— Кровати М24** — над изголовьем картины ДК7**; текстиль Т13**, Т14**, Т15**
— Ковры Т6**, Т12** — шерсть с джутом, на противоскользящей подложке
— Картины ДК4**, ДК5**, ДК7** — центр на высоте 1375–1475 мм
— Зеркала над умывальниками ДК1, ДК9, ДК10
— Шторы-волна Т1**, Т4**, Т10** (Farrow & Ball No. 201), тюль Т2**, Т5**, Т11** (Tikkurila G503) в нишах потолка
— Ваза ДК2, растение ДК6, растение ДК8

Допущения и предложения на листе. Основа листа: планировка по обводу плана заказчика, не замерена (К-1); высота до плиты 2650 мм от чистого пола — решение автора (ИЗ-1); отметки плана потолков сдвинуты на -95 мм (+2.745 плана = низ плиты), не замерено (К-2); толщины стен приняты: наружные 260 мм, перегородки 130 мм (К-1); положение стен и проёмов — по брифу без обмера и плана БТИ (К-1); разрешённая мощность 10 кВт принята, ТУ не переданы (К-6); вентканалы приняты, в брифе не заданы (К-5); тип дома, перекрытие и несущие стены не известны — документов нет (К-3); плита электрическая — принята, в брифе не указано (К-6); система заземления TN-C-S принята, ТУ не переданы (К-6); число жильцов 2 принято, в брифе не указано (К-9); подрайон климата не задан — принят не северный (жилые от 2,5 м) (К-26). Знак «**» — предложено, не утверждено (согласовать): ИЗ-2, К-7: М24. См. лист открытых вопросов (лист 5, записи К-1, К-3, К-5–К-7, К-9; лист 6, запись К-26; лист 7, запись ИЗ-2).

Настроение

Современный (контемпорари) + Тихая роскошь (quiet luxury): стены Pointing (тёплый белый, известковый шов), потолки Calla (кремовый универсальный белый); второй план — Shaded White, S 2010-Y30R, Pumice; акценты по комнатам — S 7010-Y50R, S 6020-G70Y, Bancha, Mouse's Back (К-7). Настроение стиля: актуальность, комфорт, мягкая геометрия, контраст фактур, открытость, уверенность. Свет тёплый, 2700–3000 K.

Примечания

1. Визуализации — образ интерьера. Изделия, размеры, высоты подвеса и привязки — по чертежам (план текстиля и декора — лист 59; шторы и карнизы — лист 60; ведомость текстиля — лист 61; ведомость декора и развеска — лист 62); при расхождении действуют чертежи и ведомости.
2. Коды цвета — ориентир подбора по веерам производителей; ткань утверждается по образцу при дневном свете и при свете проекта 2700–3000 K.
3. Мелкий стайлинг на визуализациях (книги, посуда, свечи) в ведомости не входит и поставляется заказчиком по желанию.

Изм.	Кол.уч	Лист	№ док.	Подп.	Дата
Разраб.		Кырлан А.С.			04.11.26
Пров.					
ГИП					
Н. контр.					
Утв.					

ГД-2026-020-АИ

Квартира 68 м², элитный модерн

Общая площадь 68,47* м² · * размеры приняты, не замерены (реестр — л. 5–7, К-1)

Дизайн-проект интерьера

Стадия	Лист	Листов
РП	58	105

Концепция декора и визуализации

М б/м


Кырлан Александр Сергеевич

выпуск 04.11.2026 № 8be4ef4c81 · стр. 65 из 117

План текстиля и декора

Шторы и карнизы, ковры, картины и зеркала, растения · размеры в мм от чистовых стен и чистого пола · марки — по ведомостям

ПРЕДВАРИТЕЛЬНО · не для производства работ · открыто пунктов: 25 (реестр — л. 5–7)

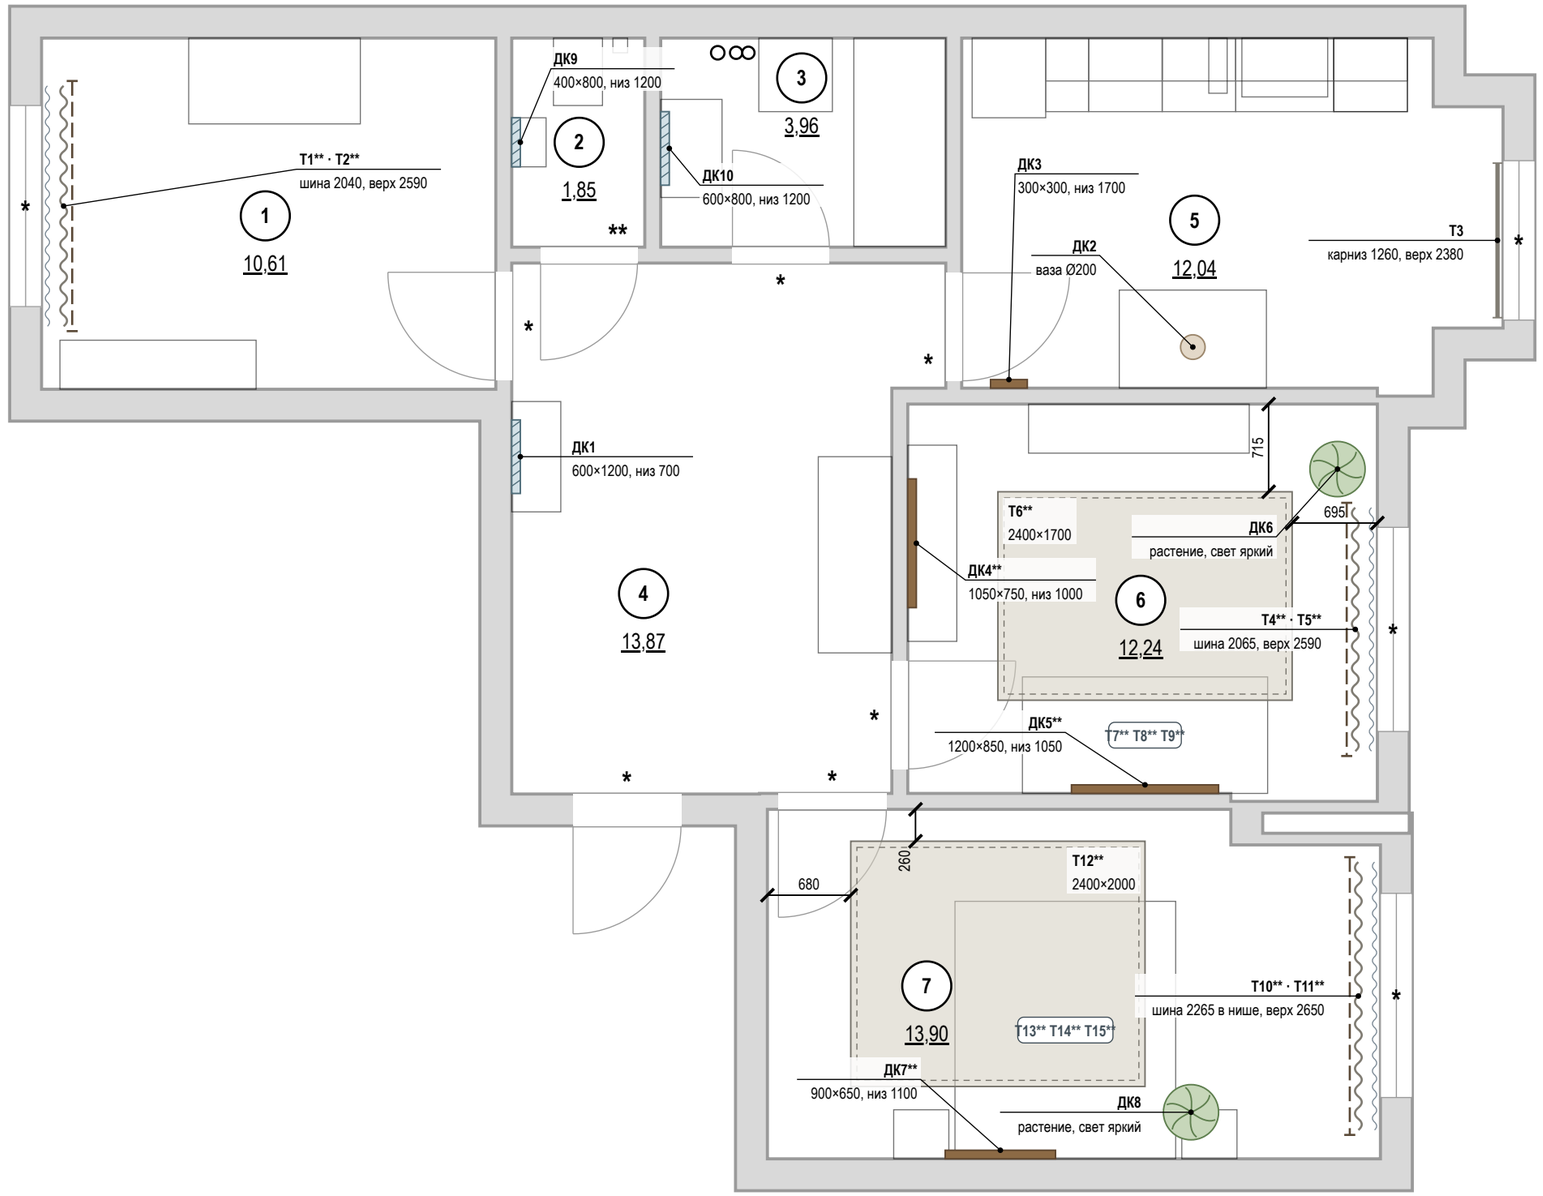

Условные обозначения

- ковёр — габарит в масштабе, цвет изделия
- шина или карниз штор (выше плоскости разреза)
- портьеры (штора-волна)
- тюль (на плане — волнистая линия)
- римская или рулонная штора в проёме
- картина на стене — ширина в масштабе
- зеркало на стене — ширина в масштабе
- растение в кашпо — диаметр в масштабе
- ваза, настольный декор
- подушки, пледы — марки на мебели
- привязка от чистовой стены, мм
- (1) номер помещения, площадь м²
- стены (подложка обмера)
- * «*» — принято, не замерено и не подтверждено
- ** «**» — предложение проектировщика, заказчиком не утверждено

Т1, ДК1 — марки по ведомостям текстиля и декора

Экспликация помещений

лист 15 · на плане — номера в марках

Окна: шина → полотно, мм

Поз.	Шина	Верх шины	Полотно, низ
Т1**, Т2**	2040	2590	2575, низ 15
Т3	1260	2380	1460, низ 920
Т4**, Т5**	2065	2590	2575, низ 15
Т10**, Т11**	2265	2650, ниша	2635, низ 15

Развеска: высоты от пола, мм

Поз.	Пом.	Ш×В	Центр	Низ	Стена
ДК1	4	600×1200	1300	700	Г
ДК3	5	300×300	1850	1700	В
ДК4**	6	1050×750	1375	1000	Г
ДК5**	6	1200×850	1475	1050	В
ДК7**	7	900×650	1425	1100	В
ДК9	2	400×800	1600	1200	Г
ДК10	3	600×800	1600	1200	Г

Примечания

1. Размеры — в мм. Отступы ковров — от чистовых стен; высоты картин и зеркал — от чистого пола до центра или низа рамы.
2. Шторы — на шинах в нишах потолка (ниша — план потолков, лист 45); закладная под шину — до обшивки ГКЛ. Схемы окон, длины полотен и сборка — лист 60.
3. Картины и зеркала массой более 5 кг — на анкеры по основанию, нагрузка крепежа не меньше двойной массы изделия; на ГКЛ — только по закладной. Декор не перекрывает розетки и выключатели.
4. Ковры на гладком полу — на противоскользящей подложке.
5. Мебель — по плану расстановки мебели (лист 19); ведомость текстиля — лист 61, ведомость декора и схемы развески — лист 62.
6. Знак «*» у проёма — допущение: положение проёма не замерено (окно пом. 1, стена Г; дверь пом. 1, стена Б; дверь пом. 3, стена В; дверь пом. 4, стена В; окно пом. 5, стена Б; дверь пом. 5, стена Г; и ещё 4); размер напечатан как принятый. Реестр: листы 5–7, вопросы К-1, К-28.
7. Номера помещений — по экспликации (лист 15); наименования и площади на этом листе не дублируются.
8. Марки текстиля «Т» и декора «Д» относятся только к листам текстиля и декора; индексы трубопроводов Т1–Т4 — на листах ВК и ОВ.

1000 мм · печать 1:1

Допущения и предложения на листе. Знак «*» принято (замерить): Ст К1-1, Ст В1-2, Ст Т3-3. Знак «**» предложено (согласовать). См. лист открытых вопросов (листы 5–7).

Изм.	Кол.уч	Лист	№ док.	Подп.	Дата
Разраб.		Кырлан А.С.			04.11.26
Пров.					
ГИП					
Н. контр.					
Утв.					

ГД-2026-020-АИ

Квартира 68 м², элитный модерн

Общая площадь 68,47* м² · * размеры приняты, не замерены (реестр — л. 5–7, К-1)

Дизайн-проект интерьера

Стадия	Лист	Листов
РП	59	105

План текстиля и декора

М 1:50

Кырлан Александр Сергеевич

выпуск 04.11.2026 № 8be4ef4c81 · стр. 66 из 117

08

Декор и текстиль


Кырлан Александр Сергеевич

выпуск 04.11.2026 № 8be4ef4c81 · стр. 67 из 117


Шторы и карнизы

Схемы окон «шина → полотно» (М 1:50) · отметки от чистого пола помещения · размеры в мм


Окно 1* — Кабинет (пом. 1): Т1, Т2** (М 1:50)**

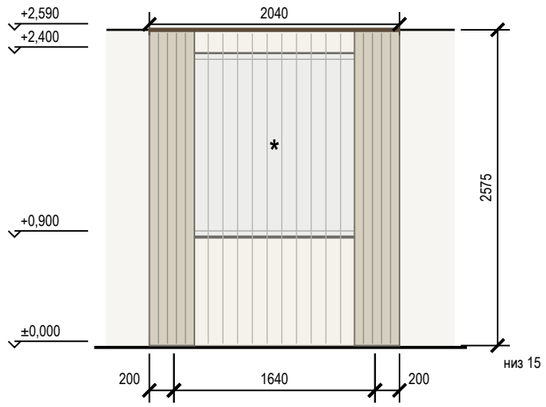


Окно 1* — Кухня-столовая (пом. 5): Т3 (М 1:50)

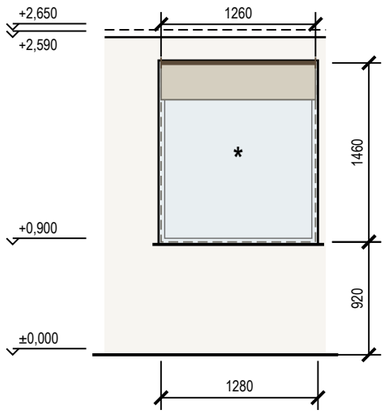

Окно 1* — Гостиная (пом. 6): Т4, Т5** (М 1:50)**

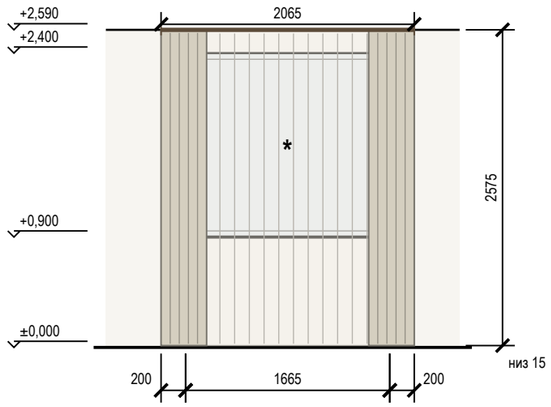

Окно 1* — Спальня (пом. 7): Т10, Т11** (М 1:50)**

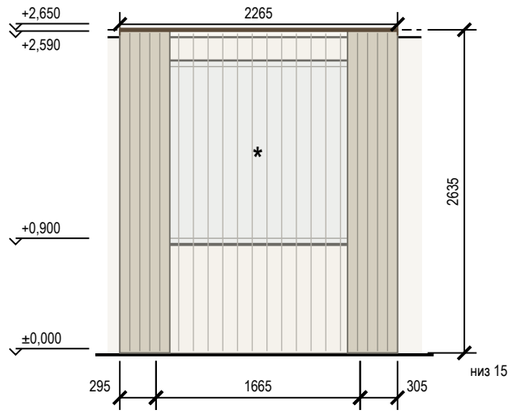

Карта окон: окно → шина → полотно

Поз.	Окно, пом.	Проём Ш×В, подоконник	Верх ниши	Изделие	Шина / карниз: длина, крепление	Верх шины	Полотно: длина, низ	Управление
Т1**	1*, пом. 1	1640×1500, подок. 900		портьеры	шина, 2040, на потолок, вынос 250	+2,590	2575, низ 15 (парит)	вручную
Т2**	1*, пом. 1	1640×1500, подок. 900		тюль	шина, 2040, на потолок, вынос 150	+2,590	2575, низ 15 (парит)	вручную
Т3	1*, пом. 5	1300×1500, подок. 900	+2,650	рулонная штора	карниз, 1260, на стену, вынос 60	+2,380	1460, низ 920	без шнура
Т4**	1*, пом. 6	1665×1500, подок. 900		портьеры	шина, 2065, на потолок, вынос 250	+2,590	2575, низ 15 (парит)	вручную
Т5**	1*, пом. 6	1665×1500, подок. 900		тюль	шина, 2065, на потолок, вынос 150	+2,590	2575, низ 15 (парит)	вручную
Т10**	1*, пом. 7	1665×1500, подок. 900	+2,650	портьеры	шина, 2265, в нише потолка, вынос 250	+2,650	2635, низ 15 (парит)	вручную
Т11**	1*, пом. 7	1665×1500, подок. 900	+2,650	тюль	шина, 2265, в нише потолка, вынос 150	+2,650	2635, низ 15 (парит)	вручную

Задания смежникам

Кому	Задание	Пом.
Гипсокартонщик	окно 1 (1665×1500, Т10**, Т11**): ниша под шторы 250×60, верх +2,650; закладная под шину L 2265 по всей длине — до обшивки	7
Электрик	выводы под электрокарнизы не требуются (управление вручную)	

Условные обозначения

- портьеры в открытом положении
- римская штора: сложена / опущена
- верх ниши под шторы в потолке
- * — «*» — принято, не замерено и не подтверждено
- тюль (на виде окна — прозрачная плашка)
- шина или карниз на отметке верха
- оконный проём

Допущения и предложения на листе

Основа листа: планировка по обводу плана заказчика, не замерена (К-1); высота до плиты 2650 мм от чистого пола — решение автора (ИЗ-1); отметки плана потолков сдвинуты на -95 мм (+2.745 плана = низ плиты), не замерено (К-2); толщины стен приняты: наружные 260 мм, перегородки 130 мм (К-1); положение стен и проёмов — по брифу без обмера и плана БТИ (К-1); разрешённая мощность 10 кВт принята, ТУ не переданы (К-6); вентканалы приняты, в брифе не заданы (К-5); тип дома, перекрытие и несущие стены не известны — документов нет (К-3); плита электрическая — принята, в брифе не указано (К-6); система заземления TN-C-S принята, ТУ не переданы (К-6); число жильцов 2 принято, в брифе не указано (К-9); подрайон климата не задан — принят не северный (жилые от 2,5 м) (К-26).

Знак «*» — принято, не замерено и не подтверждено (замерить на объекте): К-1: окно пом. 1 (стена Г), 5 (Б), 6 (Б), 7 (Б) — окно: положение, ширина, высота и подоконник приняты по обводу плана заказчика, без обмера, не замерены; дверь пом. 1 (стена Б), 5 (Г), 6 (Г), 7 (А) — проём принят по обводу плана заказчика, без обмера: положение и ширина сняты с плана, не замерены.

Знак «**» — предложение проектировщика, заказчиком не утверждено (согласовать с заказчиком): К-7: Т1, Т2, Т4, Т5, Т10, Т11.

См. лист открытых вопросов (лист 5, записи К-1, К-3, К-5–К-7, К-9; лист 6, запись К-26).

Примечания

1. Отметки — от чистого пола помещения; размеры — мм.
2. Шины в нишах потолка: закладная (брус или профиль) по всей длине ниши — до обшивки ГКЛ; ниша и её отметка — узел ниши на плане потолков (лист 45).
3. Шина в нише — на отметке верха ниши (крепление к закладной в потолке ниши); длина полотна — от верха шины до чистого пола за вычетом зазора.
4. Полотно портьер «парит» над полом на 10 мм; сборка портьер — 2,0, тюля — 2,5 (ширина полотна — в ведомости текстиля).
5. Шнур римской шторы — с натяжителем, петля низом не ниже 1500 мм от пола (защита детей; EN 13120 — рекомендация).
6. Электрокарнизы не предусмотрены; при замене на электропривод — вывод кабеля в нише у края шины (задание электрику).
7. Знак «*» у проёма — допущение: положение проёма не замерено (окно пом. 1, стена Г; окно пом. 5, стена Б; окно пом. 6, стена Б; окно пом. 7, стена Б); размер напечатан как принятый. Реестр: листы 5–7, вопрос К-1.
8. Длины шин и полотен окон 1 (пом. 1), 1 (пом. 5), 1 (пом. 6), 1 (пом. 7) выведены из размеров и положения проёма, а они — допущение: до раскроя полотен проём замерить, длины сверить.
9. Марки изделий — по плану текстиля и декора (лист 59) и ведомости текстиля (лист 61).

Изм.	Кол.уч	Лист	№ док.	Подп.	Дата				
Разраб.		Кырлан А.С.			04.11.26	ГД-2026-020-АИ			
Пров.						Квартира 68 м², элитный модерн Общая площадь 68,47* м² · * размеры приняты, не замерены (реестр — л. 5–7, К-1)			
ГИП						Дизайн-проект интерьера	Стадия: РП	Лист: 60	Листов: 105
Н. контр.						**Шторы и карнизы** М б/м	**Кырлан Александр Сергеевич**		
Утв.									

выпуск 04.11.2026 № 8be4ef4c81 · стр. 68 из 117

Ведомость текстиля

Шторы, тюль, римские шторы, ковры, подушки и пледы · размеры в мм · марки — по плану текстиля и декора

Текстиль: шторы, ковры, подушки, пледы


Поз.	Пом.	Изделие	Размер, мм	Ткань, состав, плотность	Сборка, ширина полотна		Цвет (система, код)	Кол.	Примечание
T1**	1	Портьеры в пол на потолочном карнизе, бархат (тон по комнате)	шина 2040 × полотно 2575	лён с блэкаут-подкладкой; лён / хлопок / шерсть по ткани, подкладка полиэстер; 320 г/м²	× 2, ширина 4480		Farrow & Ball No. 201 (Shaded White)	2	низ 15 (парит); на потолок
T2**	1	Тюль лён натуральный в пол	шина 2040 × полотно 2575	лён-вуаль; лён / хлопок / полиэстер по ткани	× 2,5, ширина 5600		Tikkurila G503 (Calla)	1	низ 15 (парит); на потолок
T3	5	Рулонная штора в проёме окна, ткань блэкаут	карниз 1260 × полотно 1460	полиэстер 100 %			Farrow & Ball No. 201 (Shaded White)	1	низ 920; на стену; шнур: петля —, cordless
T4**	6	Портьеры в пол на потолочном карнизе, бархат (тон по комнате)	шина 2065 × полотно 2575	шерсть плотная с подкладкой; лён / хлопок / шерсть по ткани, подкладка полиэстер; 320 г/м²	× 2, ширина 4530		Farrow & Ball No. 201 (Shaded White)	2	низ 15 (парит); на потолок
T5**	6	Тюль лён натуральный в пол	шина 2065 × полотно 2575	хлопковая кисея; лён / хлопок / полиэстер по ткани	× 2,5, ширина 5663		Tikkurila G503 (Calla)	1	низ 15 (парит); на потолок
T6**	6	Ковёр фактурный шерсть с джутом, тёплый терракотовый тон	2400×1700	шерсть с джутом; шерсть / джут / хлопок по ткани			Farrow & Ball No. 201 (Shaded White)	1	противоскользящая подложка; ворс 12 мм
T7**	6	Подушки бархат и жаккард	500×500	лён; натуральное волокно по ткани			NCS S 2010-Y30R (светлый кэмел)	3	на M20**
T8**	6	Подушки бархат и жаккард	400×600	бархат хлопковый; натуральное волокно по ткани			Farrow & Ball No. 298 (Bancha)	2	на M20**
T9**	6	Плед шерсть с бахромой, терракота	1300×1700	шерсть / хлопок по ткани			Farrow & Ball No. 298 (Bancha)	1	на M20**
T10**	7	Портьеры в пол на потолочном карнизе, бархат (тон по комнате)	шина 2265 × полотно 2635	хлопок-сатин с блэкаут-подкладкой; лён / хлопок / шерсть по ткани, подкладка полиэстер; 320 г/м²	× 2, ширина 4530		Farrow & Ball No. 201 (Shaded White)	2	низ 15 (парит); в нише потолка
T11**	7	Тюль лён натуральный в пол	шина 2265 × полотно 2635	вуаль полиэстер; лён / хлопок / полиэстер по ткани	× 2,5, ширина 5663		Tikkurila G503 (Calla)	1	низ 15 (парит); в нише потолка
T12**	7	Ковёр фактурный шерсть с джутом, тёплый терракотовый тон	2400×2000	шерсть с джутом; шерсть / джут / хлопок по ткани			Farrow & Ball No. 201 (Shaded White)	1	противоскользящая подложка; ворс 10 мм
T13**	7	Подушки бархат и жаккард	500×500	букле; натуральное волокно по ткани			NCS S 2010-Y30R (светлый кэмел)	3	на M24**
T14**	7	Подушки бархат и жаккард	400×600	хлопок-рогожка; натуральное волокно по ткани			Farrow & Ball No. 40 (Mouse's Back)	2	на M24**
T15**	7	Плед шерсть с бахромой, терракота	1300×1700	шерсть / хлопок по ткани			Farrow & Ball No. 40 (Mouse's Back)	1	на M24**

образец цвета — по HEX производителя краски, справочно

Итого: шторы и тюль — 10 шт.; ковры и дорожки — 2 шт.; подушки, пледы, покрывала — 12 шт.

Образцы по помещениям

1. Кабинет

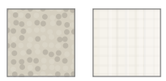


T1** T2**

5. Кухня-столовая




T3

6. Гостиная

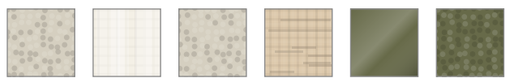

T4** T5** T6** T7** T8** T9**

7. Спальня

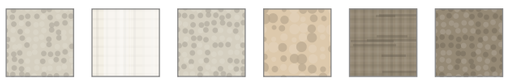

T10** T11** T12** T13** T14** T15**

Допущения и предложения на листе

Основа листа: планировка по обводу плана заказчика, не замерена (К-1); высота до плиты 2650 мм от чистого пола — решение автора (ИЗ-1); отметки плана потолков сдвинуты на -95 мм (+2.745 плана = низ плиты), не замерено (К-2); толщины стен приняты: наружные 260 мм, перегородки 130 мм (К-1); положение стен и проёмов — по брифу без обмера и плана БТИ (К-1); разрешённая мощность 10 кВт принята, ТУ не переданы (К-6); вентканалы приняты, в брифе не заданы (К-5); тип дома, перекрытие и несущие стены не известны — документов нет (К-3); плита электрическая — принята, в брифе не указано (К-6); система заземления TN-C-S принята, ТУ не переданы (К-6); число жильцов 2 принято, в брифе не указано (К-9); подрайон климата не задан — принят не северный (жилые от 2,5 м) (К-26).

Знак «**» — предложение проектировщика, заказчиком не утверждено (согласовать с заказчиком): ИЗ-2, К-7: M24 — по исходному плану: прикроватные светильники 13-А / 13-Б в 2480 мм друг от друга у стены С — двуспальная кровать 1800 по центру между ними; К-7: T1, T2, M20, T4, T5, T6, T7, T8, T9, T10, T11, T12, T13, T14, T15.

См. лист открытых вопросов (лист 5, записи К-1, К-3, К-5–К-7, К-9; лист 6, запись К-26; лист 7, запись ИЗ-2).

Примечания

1. Коды цвета — ориентир подбора по веерам производителей красок; ткань утверждается по образцу при дневном свете и при свете проекта 2700–3000 K.
2. Размеры полотен — по замеру после чистовой отделки пола и потолка; ширина полотна указана с учётом сборки, без припусков на швы. Схемы окон и отметки шин лист 60.
3. Портьеры и тюль — на тесьме «волна» по системе шины; блэкаут — подкладкой. Ковры — на противоскользящей подложке.
4. Замена изделия — аналогом по характеристикам (состав, плотность, размер, цвет по образцу) с согласованием автора проекта.
5. Места изделий — план текстиля и декора (лист 59); подушки и пледы — по марке мебели.

Изм.	Кол.уч	Лист	№ док.	Подп.	Дата
Разраб.		Кырлан А.С.			04.11.26
Пров.					
ГИП					
Н. контр.					
Утв.					

ГД-2026-020-АИ

Квартира 68 м², элитный модерн

Общая площадь 68,47* м² · * размеры приняты, не замерены (реестр — л. 5–7, К-1)

Дизайн-проект интерьера

Стадия	Лист	Листов
РП	61	105

Ведомость текстиля

М б/м

Кырлан Александр Сергеевич

выпуск 04.11.2026 № 8be4ef4c81 · стр. 69 из 117

Ведомость декора. Схемы развески

ПРЕДВАРИТЕЛЬНО · не для производства работ · открыто пунктов: 25 (реестр — л. 5–7)


Картины, зеркала, растения, настольный декор · схемы развески (М 1:50) · высоты — мм от чистого пола

Декор: картины, зеркала, растения, предметы


картина · зеркало · мебель под изделием

Поз.	Пом.	Предмет	Размер, мм	Место: стена, высота от пола, мм	Масса, кг	Крепёж и основание	Свет места, отделка	Кол.
ДК1	4	Зеркало над скамьёй 600×1200, тонкая чёрная рама	600×1200	стена Г, привязка 1279; низ 700, центр 1300; над М6**	6	дюбель 2 шт.; основание: основание стены — определить обмером до монтажа; нагрузка 20 кг		1
ДК2	5	Ваза с живыми цветами на обеденном столе	200×300	на М18** (обеденный стол)				1
ДК3	5	Часы настенные Ø300	300×300	стена В, привязка 235; низ 1700, центр 1850	1	подвес по основанию, 2 точки		1
ДК4**	6	Крупная живопись в тонкой латунной раме над консоль низкая 1600×400: крупная живопись в тонкой латунной раме: натюрморт или пейзаж в тёплых насыщенных тонах	1050×750	стена Г, привязка 610; низ 1000, центр 1375; над М23**	4	подвес по основанию, 2 точки	рама — дуб натуральный	1
ДК5**	6	Крупная живопись в тонкой латунной раме над диван 2000×950: крупная живопись в тонкой латунной раме: натюрморт или пейзаж в тёплых насыщенных тонах	1200×850	стена В, привязка 1335; низ 1050, центр 1475; над М20**	4	подвес по основанию, 2 точки	рама — дуб натуральный	1
ДК6	6	Оливковое дерево в кашпо Ø450	450×450	напольное			свет яркий рассеянный	1
ДК7**	7	Крупная живопись в тонкой латунной раме над кровать 1400×2000: крупная живопись в тонкой латунной раме: натюрморт или пейзаж в тёплых насыщенных тонах	900×650	стена В, привязка 1450; низ 1100, центр 1425; над М24**	4	подвес по основанию, 2 точки	рама — дуб натуральный	1
ДК8	7	Монстера в кашпо Ø450	450×450	напольное			свет яркий рассеянный	1
ДК9	2	Зеркало над умывальником, влагостойкое, с подсветкой	400×800	стена Г, привязка 650; низ 1200, центр 1600; над П7	5	подвес по основанию, 2 точки		1
ДК10	3	Зеркало над умывальником, влагостойкое, с подсветкой	600×800	стена Г, привязка 600; низ 1200, центр 1600; над П10**	5	подвес по основанию, 2 точки		1


ДК1 — Прихожая (пом. 4), стена Г (М 1:50)

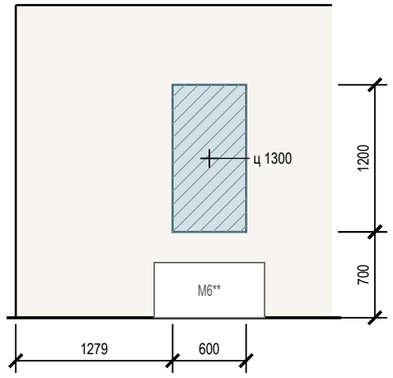


ДК3 — Кухня-столовая (пом. 5), стена В (М 1:50)

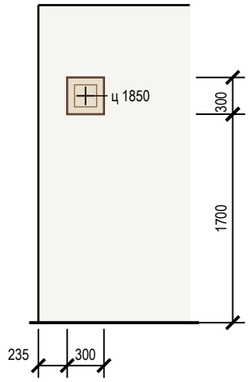


ДК4 — Гостиная (пом. 6), стена Г (М 1:50)**

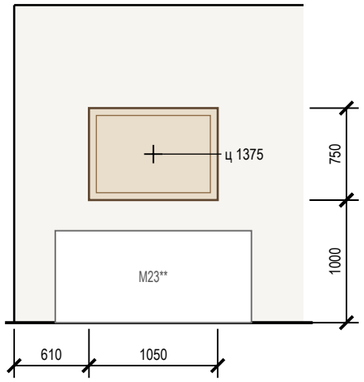

ДК5 — Гостиная (пом. 6), стена В (М 1:50)**

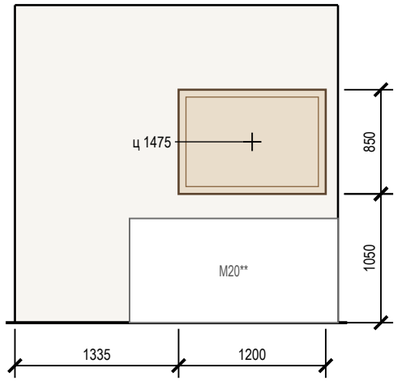

ДК7 — Спальня (пом. 7), стена В (М 1:50)**

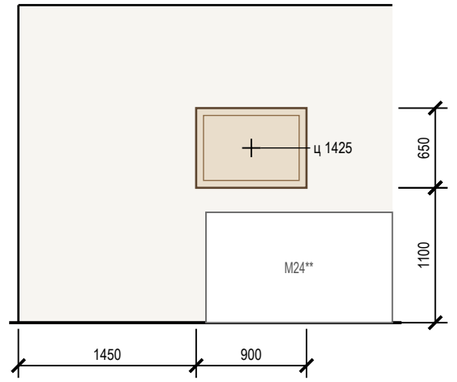

Допущения и предложения на листе

Основа листа: планировка по обводу плана заказчика, не замерена (К-1); высота до плиты 2650 мм от чистого пола — решение автора (ИЗ-1); отметки плана потолков сдвинуты на -95 мм (+2.745 плана = низ плиты), не замерено (К-2); толщины стен приняты: наружные 260 мм, перегородки 130 мм (К-1); положение стен и проёмов — по брифу без обмера и плана БТИ (К-1); разрешённая мощность 10 кВт принята, ТУ не переданы (К-6); вентканалы приняты, в брифе не заданы (К-5); тип дома, перекрытие и несущие стены не известны — документов нет (К-3); плита электрическая — принята, в брифе не указано (К-6); система заземления TN-C-S принята, ТУ не переданы (К-6); число жильцов 2 принято, в брифе не указано (К-9); подрайон климата не задан — принят не северный (жилые от 2,5 м) (К-26).

Знак «**» — предложение проектировщика, заказчиком не утверждено (согласовать с заказчиком): М6 — сушилка для обуви под скамьёй — предложение по умолчанию (комфорт), заказчик может снять; питание — розетка «уборка, сушилка обуви»; ИЗ-2, К-7: М24 — по исходному плану: прикроватные светильники 13-А / 13-Б в 2480 мм друг от друга у стены С — двуспальная кровать 1800 по центру между ними; ИЗ-3, К-7: П10 — раковина у левой стены: светильники 14 плана — у зеркала над ней; отвод К1 к стояку в углу короткий; К-7: М18, М20, М23, ДК4, ДК5, ДК7.

См. лист открытых вопросов (лист 5, записи К-1, К-3, К-5–К-7, К-9; лист 6, запись К-26; лист 7, записи ИЗ-2, ИЗ-3).

Примечания

1. Высоты — от чистого пола помещения до низа изделия, «ц» — до центра; привязки — от чистовой грани угла стены, мм.
2. Над мебелью низ изделия — на 150–250 мм выше спинки или изголовья; без мебели центр — на 1450–1600 мм от пола.
3. Изделия до 5 кг — на два подвеса по основанию; тяжелее — на анкеры с нагрузкой не меньше двойной массы; на ГКЛ — только по закладной или анкеру для пустотелых оснований.
4. Зеркала в рост — с креплением от опрокидывания; в санузлах — влагостойкие, на клей для зеркал и нейтральный силикон.
5. Места изделий — план текстиля и декора (лист 59). Схемы развески остальных изделий — лист 63.

Изм.	Кол.уч	Лист	№ док.	Подп.	Дата
Разраб.		Кырлан А.С.			04.11.26
Пров.					
ГИП					
Н. контр.					
Утв.					

ГД-2026-020-АИ

Квартира 68 м², элитный модерн

Общая площадь 68,47* м² · * размеры приняты, не замерены (реестр — л. 5–7, К-1)

Дизайн-проект интерьера

Стадия	Лист	Листов
РП	62	105

Ведомость декора. Схемы развески

М б/м

Кырлан Александр Сергеевич

выпуск 04.11.2026 № 8be4ef4c81 · стр. 70 из 117

Схемы развески (продолжение)


Схемы развески картин и зеркал (М 1:50) · высоты — мм от чистого пола

ПРЕДВАРИТЕЛЬНО · не для производства работ · открыто пунктов: 25 (реестр — л. 5–7)


Ведомость декора (размер, масса, крепёж и основание) — лист 62

картина · зеркало · мебель под изделием

ДК9 — Санузел (пом. 2), стена Г (М 1:50)

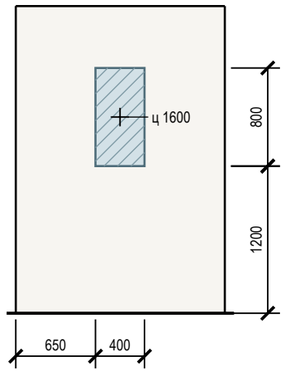

ДК10 — Ванная (пом. 3), стена Г (М 1:50)

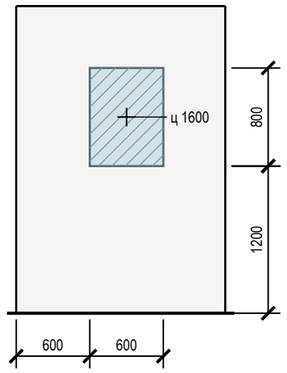

Допущения и предложения на листе

Основа листа: планировка по обводу плана заказчика, не замерена (К-1); высота до плиты 2650 мм от чистого пола — решение автора (ИЗ-1); отметки плана потолков сдвинуты на -95 мм (+2.745 плана = низ плиты), не замерено (К-2); толщины стен приняты: наружные 260 мм, перегородки 130 мм (К-1); положение стен и проёмов — по брифу без обмера и плана БТИ (К-1); разрешённая мощность 10 кВт принята, ТУ не переданы (К-6); вентканалы приняты, в брифе не заданы (К-5); тип дома, перекрытие и несущие стены не известны — документов нет (К-3); плита электрическая — принята, в брифе не указано (К-6); система заземления TN-C-S принята, ТУ не переданы (К-6); число жильцов 2 принято, в брифе не указано (К-9); подрайон климата не задан — принят не северный (жилые от 2,5 м) (К-26).

См. лист открытых вопросов (лист 5, записи К-1, К-3, К-5, К-6, К-9; лист 6, запись К-26).

Примечания

1. Высоты — от чистого пола помещения до низа изделия, «ц» — до центра; привязки — от чистовой грани угла стены, мм.
2. Над мебелью низ изделия — на 150–250 мм выше спинки или изголовья; без мебели центр — на 1450–1600 мм от пола.
3. Изделия до 5 кг — на два подвеса по основанию; тяжелее — на анкеры с нагрузкой не меньше двойной массы; на ГКЛ — только по закладной или анкеру для пустотелых оснований.
4. Зеркала в рост — с креплением от опрокидывания; в санузлах — влагостойкие, на клей для зеркал и нейтральный силикон.
5. Места изделий — план текстиля и декора (лист 59). Ведомость декора: размер, масса, крепёж и основание — лист 62.

Изм.	Кол.уч	Лист	№ док.	Подп.	Дата
Разраб.		Кырлан А.С.			04.11.26
Пров.					
ГИП					
Н. контр.					
Утв.					

ГД-2026-020-АИ

Квартира 68 м², элитный модерн

Общая площадь 68,47* м² · * размеры приняты, не замерены (реестр — л. 5–7, К-1)

Дизайн-проект интерьера

Стадия	Лист	Листов
РП	63	105

Схемы развески (продолжение)

М б/м


Кырлан Александр Сергеевич

выпуск 04.11.2026 № 8be4ef4c81 · стр. 71 из 117

Встроенная мебель. Схема расположения

встроенная и корпусная мебель на заказ, кухонный гарнитур · размеры в мм · марки — по ведомости изделий

ПРЕДВАРИТЕЛЬНО · не для производства работ · открыто пунктов: 25 (реестр — л. 5–7)

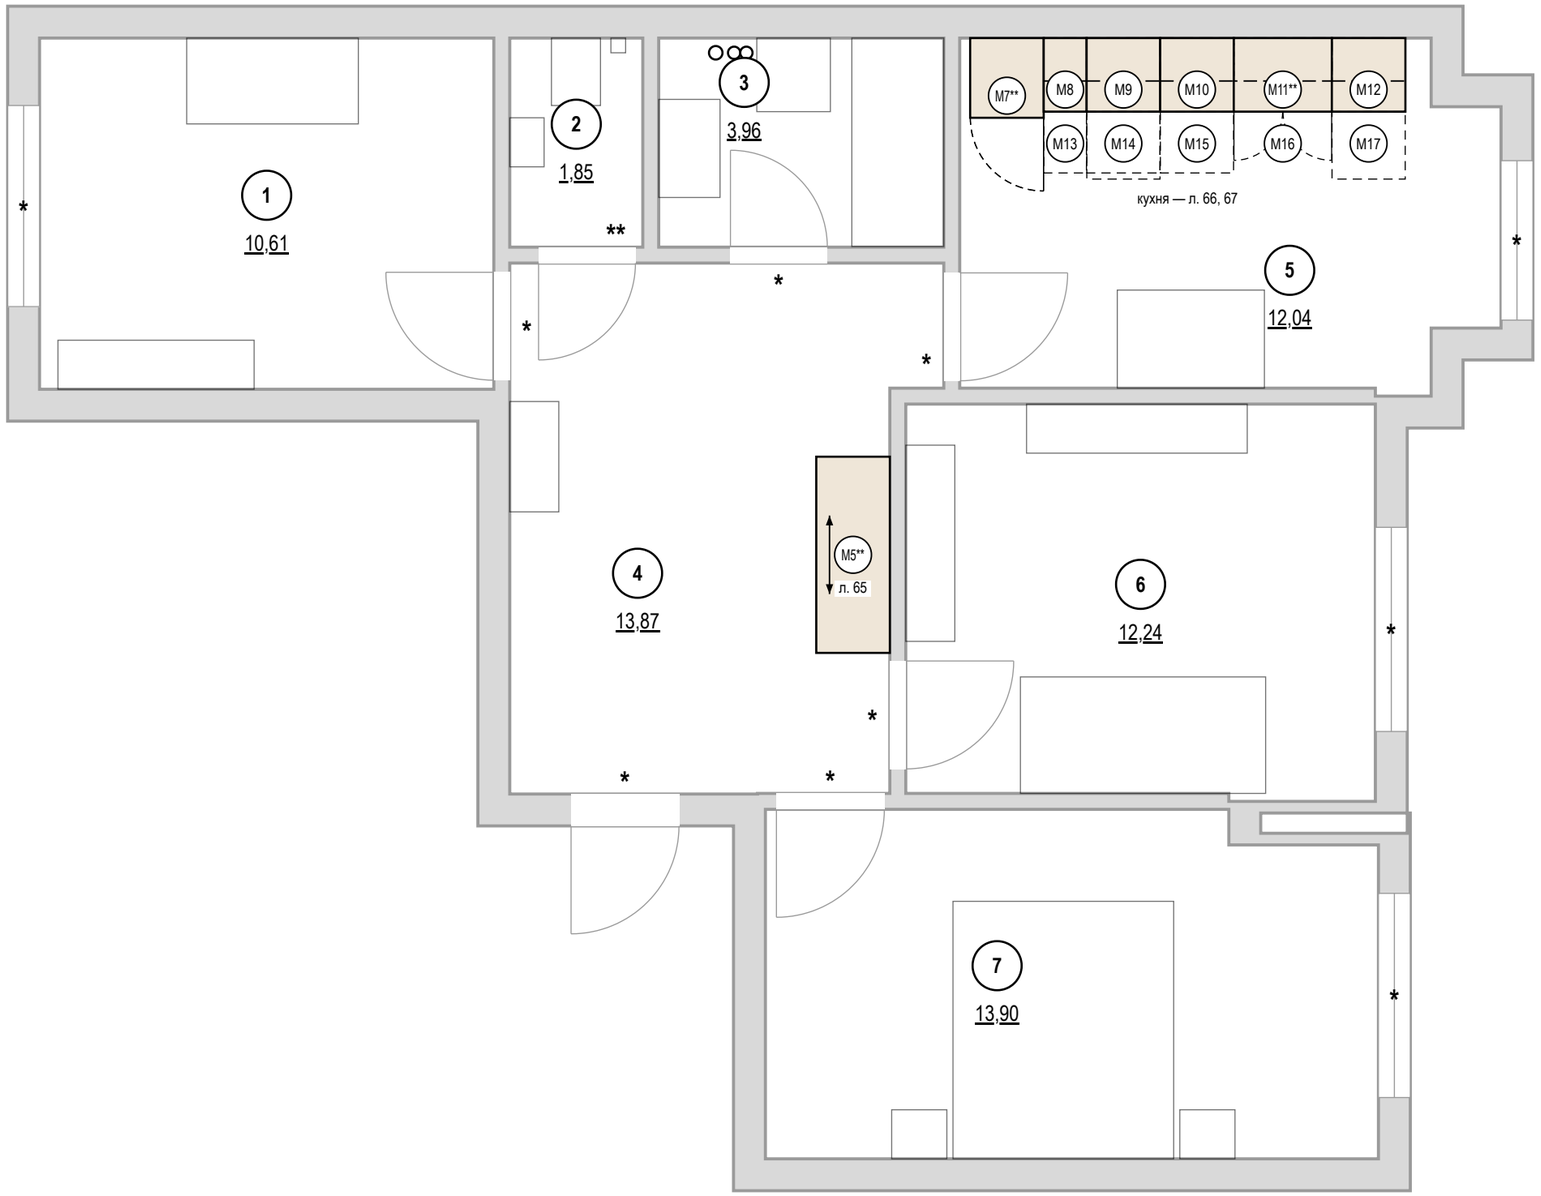

Ведомость изделий

Марка	Наименование	Пом.	Ш×Г×В, мм	Лист
M5**	Шкаф-купе	4	1600×600×2450	65
M7**	Пенал: холодильник встр.	5	600×650×2200	66
M8	Модуль нижний: ящики	5	350×600×900	66
M13	Модуль навесной: полки	5	350×350×900	66
M9	Модуль нижний: духовой шкаф, варочная	5	600×600×900	66
M14	Модуль навесной: полки	5	600×350×800	66
M10	Модуль нижний: ящики	5	600×600×900	66
M15	Модуль навесной: полки	5	600×350×900	66
M11**	Модуль нижний: мойка	5	800×600×900	66
M16	Модуль навесной: сушка	5	800×350×900	66
M12	Модуль под ПММ 60: без корпуса, фасад на дверь машины	5	600×600×900	66
M17	Модуль навесной: полки	5	600×350×900	66

Условные обозначения

- изделие мебельщика: корпус на полу
- невидимый контур: навесной модуль, корпус под столешницей
- открывание распашного фасада
- зона выдвижения ящика, двери техники
- дверь купе, стрелка — направление движения
- К1 — марка изделия или модуля (на схеме расположения под ней — лист изделия)
- * — «*» — принято, не замерено и не подтверждено
- ** — «**» — предложение проектировщика, заказчиком не утверждено

Допущения и предложения на листе. Основа листа: планировка по обводу плана заказчика, не замерена (К-1); высота до плиты 2650 мм от чистого пола — решение автора (ИЗ-1); отметки плана потолков сдвинуты на -95 мм (+2.745 плана = низ плиты), не замерено (К-2); толщины стен приняты: наружные 260 мм, перегородки 130 мм (К-1); положение стен и проёмов — по брифу без обмера и плана БТИ (К-1); разрешённая мощность 10 кВт принята, ТУ не переданы (К-6); вентканалы приняты, в брифе не заданы (К-5); тип дома, перекрытие и несущие стены не известны — документов нет (К-3); плита электрическая — принята, в брифе не указано (К-6); система заземления TN-C-S принята, ТУ не переданы (К-6); число жильцов 2 принято, в брифе не указано (К-9); подрайон климата не задан — принят не северный (жилые от 2,5 м) (К-26). Знак «*» — принято, не замерено (замерить): К-4: Ст К1-1, Ст В1-2, Ст ТЗ-3. Знак «**» — предложено, не утверждено (согласовать). См. лист открытых вопросов (лист 5, записи К-1, К-3–К-9; лист 6, запись К-26).

Примечания

1. Изделия — по чистовым размерам помещений; перед раскроем — контрольный замер цеха после чистовой отделки стен, пола и потолка.
2. Открывание фасадов и выдвижение ящиков показано в открытом положении: зоны не пересекают двери, радиаторы, выключатели и проходы.
3. Стояки и счётчики за мебелью — с сервисным люком; газовые трубы мебелью не зашиваются.
4. Покупная мебель — по плану расстановки мебели и спецификации дизайнера; здесь — подложкой.
5. Знак «*» у проёма — положение не замерено; реестр: листы 5–7, вопросы К-1, К-28.

1000 мм · печать 1:1

Изм.	Кол.уч	Лист	№ док.	Подп.	Дата
Разраб.		Кырлан А.С.			04.11.26
Пров.					
ГИП					
Н. контр.					
Утв.					

ГД-2026-020-АИ

Квартира 68 м², элитный модерн

Общая площадь 68,47* м² · * размеры приняты, не замерены (реестр — л. 5–7, К-1)

Дизайн-проект интерьера	Стадия	Лист	Листов
	РП	64	105

Встроенная мебель. Схема расположения

М 1:50

Кырлан Александр Сергеевич


выпуск 04.11.2026 № 8be4ef4c81 · стр. 72 из 117

Шкаф-купе М5


Прихожая (пом. 4) · вид из помещения · размеры в мм, отметки в м

ПРЕДВАРИТЕЛЬНО · не для производства работ · открыто пунктов: 25 (реестр — л. 5–7)


Вид с фасадами

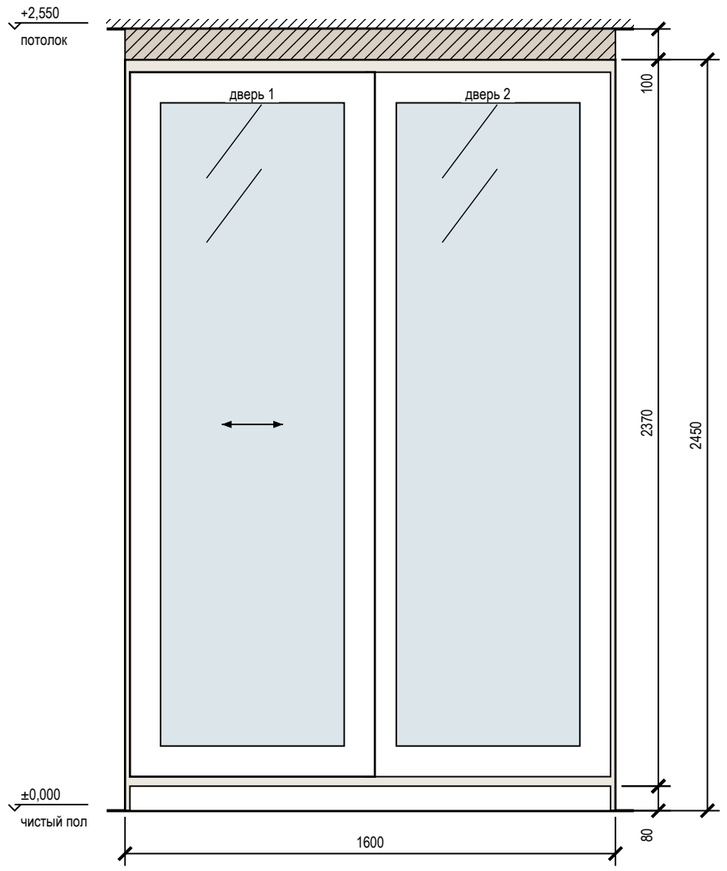


Вид без фасадов

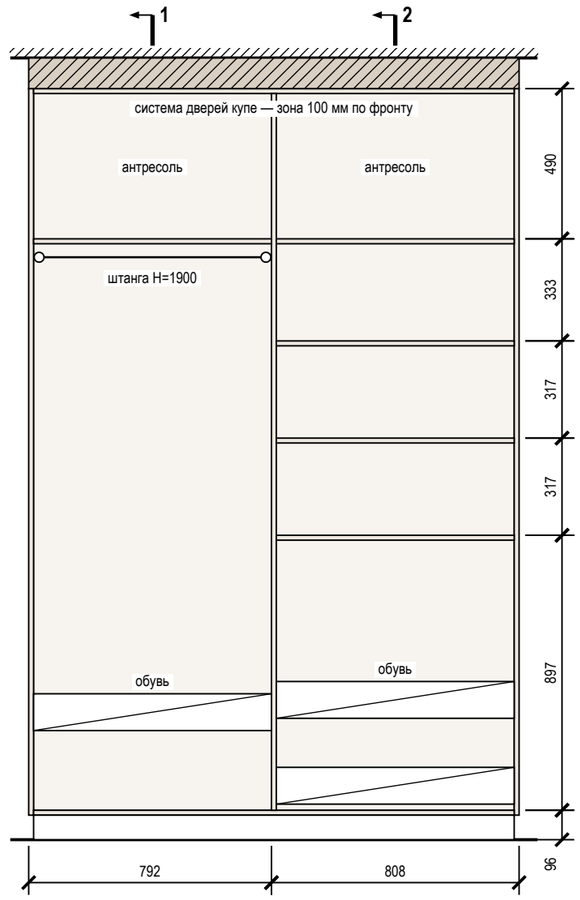

Разрез 1-1

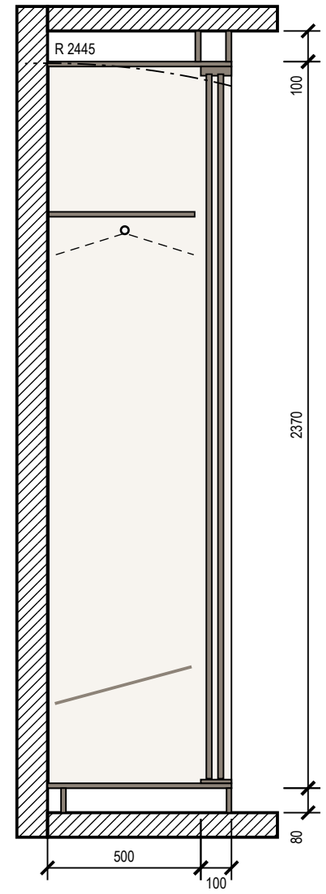

Разрез 2-2

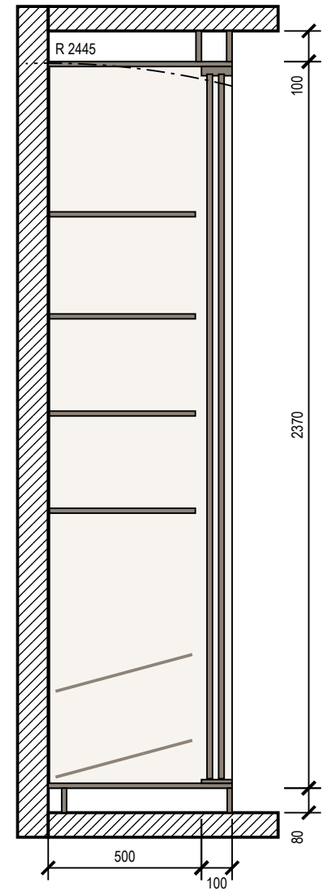

Примечания

1. Размеры — в мм по чистовой отделке; изделие 1600×600×2450 (Ш×Г×В). Перед раскроем — контрольный замер цеха после чистовой отделки стен, пола и потолка.
2. Корпус — ЛДСП 16 мм, задняя стенка ХДФ 4 мм в паз, цоколь 80 мм на регулируемых опорах; двери купе — МДФ, шпон / эмаль 18 мм; вставка — зеркало серебро 4 мм на безопасной плёнке, в профиле двери; нахлёст 30 мм, ширина двери 799 мм, высота — проём минус 40 мм; цвет — по колерной карте.
3. Кромка: скрытые торцы 0,4 мм, видимые 1 мм (ПВХ/АБС).
4. Номинальные зазоры: дверь купе — боковина 3 мм, фасад ящика — стойка 2 мм; ящики внутри купе — с накладкой 30 мм на стойке со стороны нахлёста дверей.
5. Присадка по 32-й системе — выполняет цех.
6. Компенсатор 100 мм — короб из ЛДСП по фронту и торцам, подгоняется к потолку при монтаже (припуск 20 мм), крепится к корпусу и к потолку.
7. Подъём корпуса: диагональ боковины без цоколя √(2370² + 600²) = 2445 мм < 2550 мм до потолка — корпус собирается лёжа, поднимается поворотом и ставится на цоколь.
8. Крепление к стене от опрокидывания — уголки 2 шт. к несущему основанию (монтажная схема шкафов).

Условные обозначения

- дверь купе, стрелка — направление движения
- корпус и полки ЛДСП (вид на стену)
- задняя стенка ХДФ
- деталь в разрезе
- компенсатор — короб до потолка
- зеркальная вставка фасада
- штанга для плечиков (на разрезе — плечики 450 мм)
- траектория угла корпуса при подъёме в проектное положение

Допущения и предложения на листе

Основа листа: планировка по обводу плана заказчика, не замерена (К-1); высота до плиты 2650 мм от чистого пола — решение автора (ИЗ-1); отметки плана потолков сдвинуты на -95 мм (+2.745 плана = низ плиты), не замерено (К-2); толщины стен приняты: наружные 260 мм, перегородки 130 мм (К-1); положение стен и проёмов — по брифу без обмера и плана БТИ (К-1); разрешённая мощность 10 кВт принята, ТУ не переданы (К-6); вентканалы приняты, в брифе не заданы (К-5); тип дома, перекрытие и несущие стены не известны — документов нет (К-3); плита электрическая — принята, в брифе не указано (К-6); система заземления TN-C-S принята, ТУ не переданы (К-6); число жильцов 2 принято, в брифе не указано (К-9); подрайон климата не задан — принят не северный (жилые от 2,5 м) (К-26).
См. лист открытых вопросов (лист 5, записи К-1, К-3, К-5, К-6, К-9; лист 6, запись К-26).

1000 мм · печать 1:1

Изм.	Кол.уч	Лист	№ док.	Подп.	Дата
Разраб.		Кырлан А.С.			04.11.26
Пров.					
ГИП					
Н. контр.					
Утв.					

ГД-2026-020-АИ

Квартира 68 м², элитный модерн

Общая площадь 68,47* м² · * размеры приняты, не замерены (реестр — л. 5–7, К-1)

Дизайн-проект интерьера

Стадия	Лист	Листов
РП	65	105

Шкаф-купе М5

М 1:20

Кырлан Александр Сергеевич


выпуск 04.11.2026 № 8be4ef4c81 · стр. 73 из 117

Кухня (пом. 5). Развёртка гарнитура


Кухня-столовая (пом. 5) · стена А · вид из помещения · размеры в мм, отметки в м

ПРЕДВАРИТЕЛЬНО · не для производства работ · открыто пунктов: 25 (реестр — л. 5–7)


Вид с фасадами

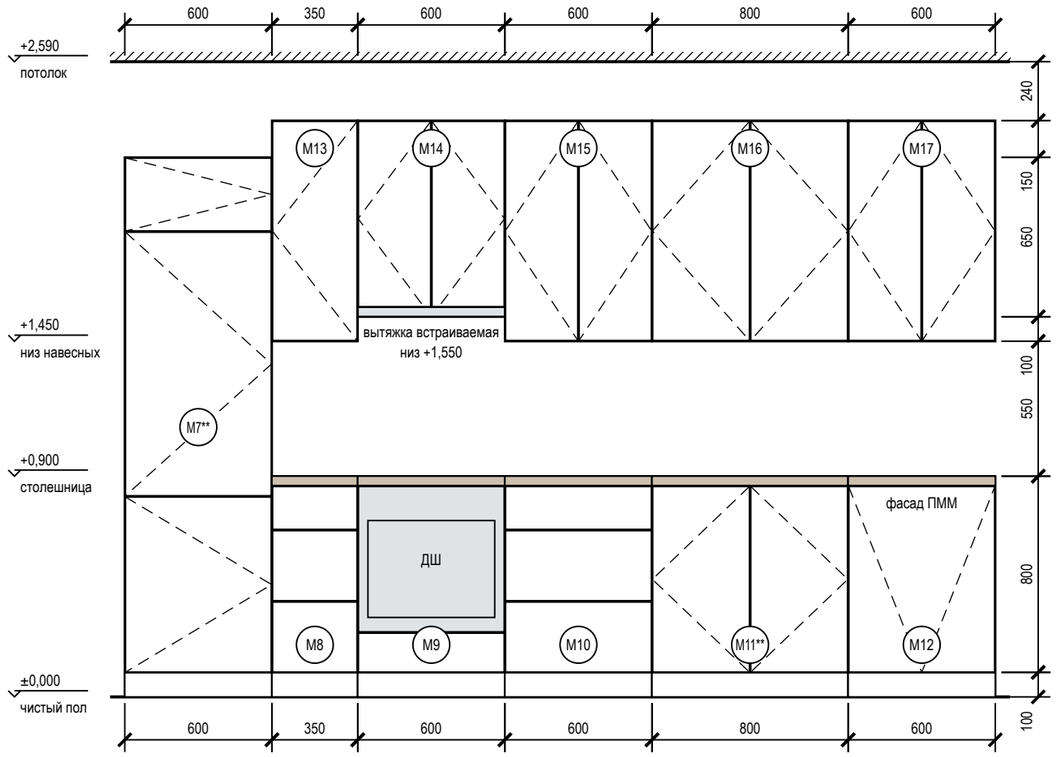


Вид без фасадов (наполнение, выводы)

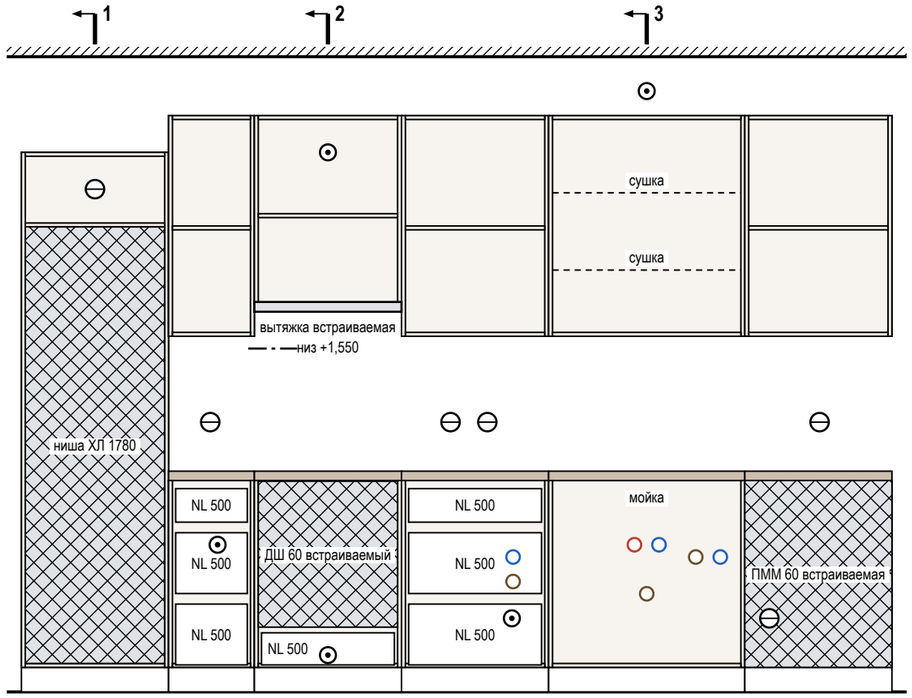


Разрез 1-1

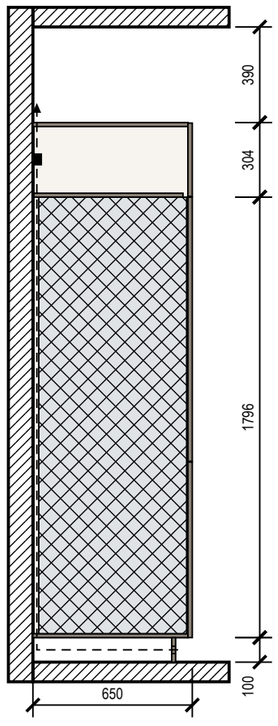

Разрез 2-2

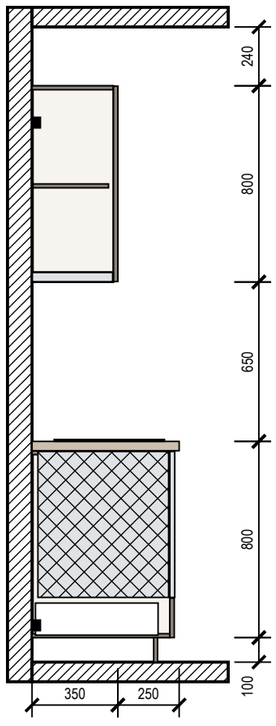

Разрез 3-3

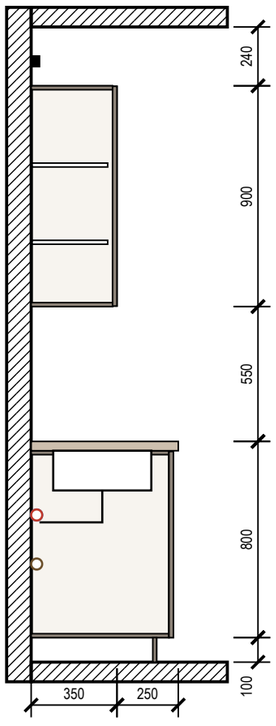

1000 мм · печать 1:1

Условные обозначения

- фасад распашной: линии сходятся к стороне петель
- фасад ящика, карго
- встраиваемая техника
- столешница
- доборная планка
- деталь в разрезе
- K1 — марка изделия или модуля (на схеме расположения под ней — лист изделия)
- розетка на стене
- вывод кабеля к технике
- B1 — вывод воды В1 / Т3, канализации К1

Примечания

1. Размеры — в мм по чистовой отделке, вид из помещения; марки — как на плане расстановки. Перед раскроем — контрольный замер цеха после фартука и пола.
2. Корпуса — ЛДСП 16 мм, задняя стенка ХДФ 4 мм; фасады — МДФ: шпон американского ореха (нижние модули) и эмаль пыльно-синяя с узкой филёнкой (колонны), латунные ручки-скобы 18 мм, цвет по колерной карте; столешница 38 мм, свес 20 мм; цоколь 100 мм.
3. Кромка: скрытые торцы 0,4 мм, видимые 1 мм. Номинальные зазоры: между фасадами 3 мм, фасад — столешница 3 мм, фасад — стена не менее 3 мм.
4. Ящики полного выдвижения и петли — с доводчиком; присадка по 32-й системе — выполняет цех.
5. Вытяжка встраивается в дно навесного модуля M14 над варочной: её низ на 1550 мм от пола, 650 мм над панелью (не меньше 650 мм).
6. Ниши техники (холодильник — ориентир 1780 мм) — по монтажным схемам выбранных моделей: решётка в цоколе и канал за пеналом холодильника, зазор за духовым шкафом, фасад ПММ на двери машины.

Допущения и предложения на листе

Основа листа: планировка по обводу плана заказчика, не замерена (К-1); высота до плиты 2650 мм от чистого пола — решение автора (ИЗ-1); отметки плана потолков сдвинуты на -95 мм (+2.745 плана = низ плиты), не замерено (К-2); толщины стен приняты: наружные 260 мм, перегородки 130 мм (К-1); положение стен и проёмов — по брифу без обмера и плана БТИ (К-1); разрешённая мощность 10 кВт принята, ТУ не переданы (К-6); вентканалы приняты, в брифе не заданы (К-5); тип дома, перекрытие и несущие стены не известны — документов нет (К-3); плита электрическая — принята, в брифе не указано (К-6); система заземления TN-C-S принята, ТУ не переданы (К-6); число жильцов 2 принято, в брифе не указано (К-9); подрайон климата не задан — принят не северный (жилые от 2,5 м) (К-26).

Знак «**» — предложение проектировщика, заказчиком не утверждено (согласовать с заказчиком): К-7: M7, M11.

См. лист открытых вопросов (лист 5, записи К-1, К-3, К-5–К-7, К-9; лист 6, запись К-26).

Изм.	Кол.уч	Лист	№ док.	Подп.	Дата
Разраб.		Кырлан А.С.			04.11.26
Пров.					
ГИП					
Н. контр.					
Утв.					

ГД-2026-020-АИ

Квартира 68 м², элитный модерн

Общая площадь 68,47* м² · * размеры приняты, не замерены (реестр — л. 5–7, К-1)

Дизайн-проект интерьера

Стадия	Лист	Листов
РП	66	105

Кухня (пом. 5). Развёртка гарнитура

М 1:25

Кырлан Александр Сергеевич


выпуск 04.11.2026 № 8be4ef4c81 · стр. 74 из 117

Кухня (пом. 5). Монтажная схема


Кухня-столовая (пом. 5) · стена А · размеры в мм от чистых поверхностей, высоты — от чистого пола

ПРЕДВАРИТЕЛЬНО · не для производства работ · открыто пунктов: 25 (реестр — л. 5–7)

Привязка выводов и крепление модулей

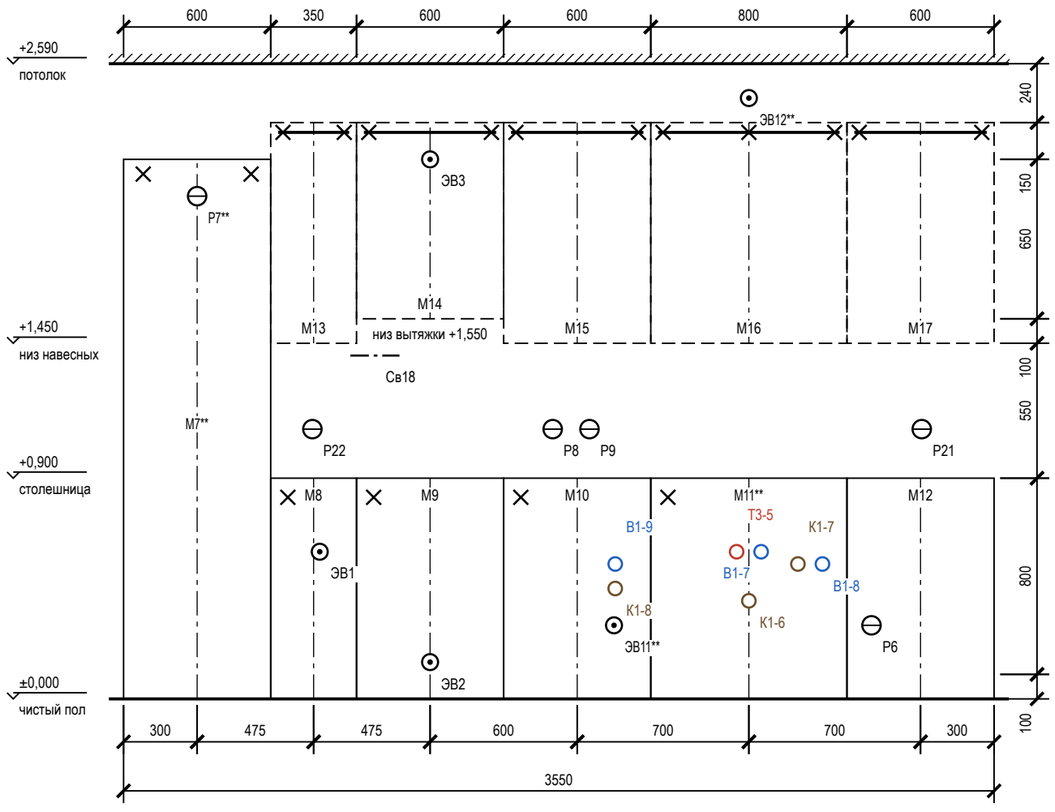

План столешницы

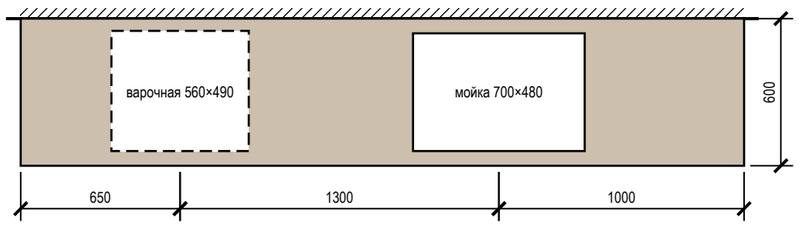

Привязка выводов к осям модулей

Код	Назначение	Модуль	От оси, мм	Н, мм	Размещение
Р7**	розетка — холодильник — над нишей, съёмная панель	М7**	0	2050	над нишей холодильника, съёмная панель
Р22	розетка ×2 — фартук	М8	−5	1100	над столешницей (фартук)
ЭВ1	вывод кабеля — варочная панель — в соседнем модуле, за ящиком	М8	+25	600	в соседнем модуле, за ящиком
Св18	светодиодная лента — марка 13 по исходному плану: «підсвітка робочої поверхні»	М9	−225	1400	над столешницей (фартук)
ЭВ2	вывод кабеля — духовой шкаф — в цоколе	М9	0	150	под духовым шкафом, доступ через ящик
ЭВ3	вывод кабеля — вытяжка — над корпусом	М14	0	2200	в навесном модуле
Р8	розетка ×2 — чайник и кофемашина (отдельная линия)	М10	−100	1100	над столешницей (фартук)
Р9	розетка — фартук: мелкая техника	М10	+50	1100	над столешницей (фартук)
ЭВ11**	вывод кабеля — измельчитель мойки	М10	+150	300	в соседнем модуле, за ящиком
В1-9	В1 — ro-filter	М10	+155	550	в соседнем модуле, за ящиком
К1-8	К1 Ø40 — ro-filter	М10	+155	450	в соседнем модуле, за ящиком
Т3-5	Т3 — межос. 100	М11**	−50	600	в модуле мойки
ЭВ12**	вывод кабеля — подсветка навесных шкафов (блок питания ленты)	М16	0	2450	в навесном модуле
К1-6	К1 Ø50 — мойка	М11**	0	400	в модуле мойки
В1-7	В1 — межос. 100	М11**	+50	600	в модуле мойки
К1-7	К1 Ø40 — слив ПММ в шкафу мойки	М11**	+200	550	в модуле мойки
В1-8	В1 — кран ПММ в шкафу мойки	М11**	+300	550	в модуле мойки
Р6	розетка — посудомоечная машина (в нише М12, сбоку от корпуса, доступ через цоколь)	М12	−200	300	за ПММ — перенести в соседний модуль
Р21	розетка ×2 — фартук	М12	+5	1100	над столешницей (фартук)

Зазоры под отделку

Поверхность	Отделка	Зазор, мм	Учесть
фартук	керамогранит	10	от чернового основания до корпуса навесных и столешницы
стены	окраска	5	под штукатурку и шпаклёвку за пеналом
пол	инженерная доска		цоколь — после укладки пола, опоры ±20 мм

Примечания

1. Выводы — по проекту электрики и ВК; привязка по горизонтали — от оси модуля (плюс — вправо по виду), по высоте — от чистого пола до оси вывода.
2. Пенал — уголки к стене 2 шт. сверху; нижние модули — стяжками между собой и уголком к стене; ряд выставить по уровню опорами цоколя.
3. Розетки над столешницей — не ниже 150 мм над ней и не за корпусом техники; розетка за ПММ, духовым шкафом и холодильником — только в соседнем модуле или в зоне цоколя с доступом.
4. Столешница — вырезы по шаблонам выбранных моделей мойки и варочной панели; торцы у стены — герметик, пристеночный плинтус.

Условные обозначения

- нижний модуль, пенал (контур)
- невидимый контур: навесной модуль, корпус под столешницей
- ось модуля (от неё — привязка вывода)
- анкер / уголок крепления к стене
- розетка на стене
- вывод кабеля к технике
- B1 — вывод воды В1 / Т3, канализации К1

Допущения и предложения на листе. Знак «**» предложено (согласовать). См. лист открытых вопросов (листы 5–7).

1000 мм · печать 1:1

Изм.	Кол.уч	Лист	№ док.	Подп.	Дата
Разраб.		Кырлан А.С.			04.11.26
Пров.					
ГИП					
Н. контр.					
Утв.					

ГД-2026-020-АИ

Квартира 68 м², элитный модерн

Общая площадь 68,47* м² · * размеры приняты, не замерены (реестр — л. 5–7, К-1)

Дизайн-проект интерьера

Стадия	Лист	Листов
РП	67	105

Кухня (пом. 5). Монтажная схема

М 1:25


Кырлан Александр Сергеевич

выпуск 04.11.2026 № 8be4ef4c81 · стр. 75 из 117

Шкафы. Монтажная схема

крепление к стене, установочные размеры, зазоры под отделку · размеры в мм

Шкаф-купе М5 (пом. 4)**

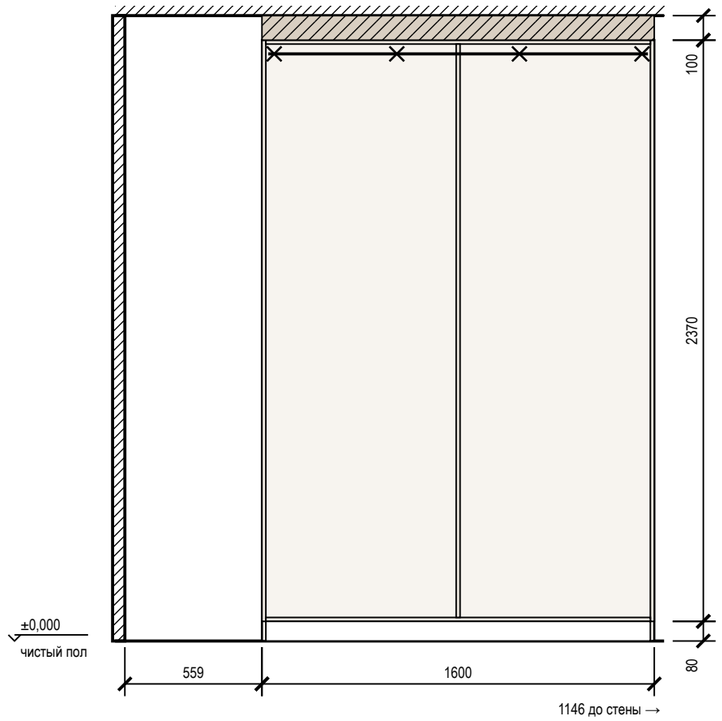

Крепление и зазоры под отделку

Марка	Помещение, стена	Основание	Отделка стены	Зазор, мм	Крепёж по планке	От опрокидывания
М5**	Прихожая (4), стена Б	по основанию — см. таблицу крепежа	окраска	5	анкер 4 шт., шаг 500	уголки 2 шт.

Крепёж по основанию стены

Основание стены	Крепёж
бетон, ж/б	анкер-шуруп 7,5×72 или дюбель 8×60 с шурупом 5×70
кирпич полнотелый	дюбель 8×80 с шурупом 5×90
газобетон, пазогребень	дюбель для газобетона 10×100 или химический анкер
гипсокартон	закладная до обшивки (брус 40×80 или фанера 18 мм), саморез в закладную

Условные обозначения

- анкер / уголок крепления к стене
- корпус и полки ЛДСП (вид на стену)
- компенсатор — короб до потолка

Примечания

1. Установочные размеры — от чистого пола и чистых стен; перед установкой контрольный замер после отделки.
2. Порядок: корпус выставить по уровню опорами цоколя → закрепить к стене по задней планке → навесить двери и фасады, отрегулировать зазоры → подогнать и закрепить компенсатор.
3. Анкеры — с шагом не более 500 мм, не ближе 50 мм от края планки; на ГКЛ только в закладную, установленную до обшивки.
4. Скрытые коммуникации под анкеры проверить детектором; трассы электрики по плану розеток.

Допущения и предложения на листе

Основа листа: планировка по обводу плана заказчика, не замерена (К-1); высота до плиты 2650 мм от чистого пола — решение автора (ИЗ-1); отметки плана потолков сдвинуты на -95 мм (+2.745 плана = низ плиты), не замерено (К-2); толщины стен приняты: наружные 260 мм, перегородки 130 мм (К-1); положение стен и проёмов — по брифу без обмера и плана БТИ (К-1); разрешённая мощность 10 кВт принята, ТУ не переданы (К-6); вентканалы приняты, в брифе не заданы (К-5); тип дома, перекрытие и несущие стены не известны — документов нет (К-3); плита электрическая — принята, в брифе не указано (К-6); система заземления TN-C-S принята, ТУ не переданы (К-6); число жильцов 2 принято, в брифе не указано (К-9); подрайон климата не задан — принят не северный (жилые от 2,5 м) (К-26).
Знак «**» — предложение проектировщика, заказчиком не утверждено (согласовать с заказчиком): К-7: М5.
См. лист открытых вопросов (лист 5, записи К-1, К-3, К-5–К-7, К-9; лист 6, запись К-26).

1000 мм · печать 1:1

Изм.	Кол.уч	Лист	№ док.	Подп.	Дата
Разраб.		Кырлан А.С.			04.11.26
Пров.					
ГИП					
Н. контр.					
Утв.					

ГД-2026-020-АИ

Квартира 68 м², элитный модерн

Общая площадь 68,47* м² · * размеры приняты, не замерены (реестр — л. 5–7, К-1)

Дизайн-проект интерьера

Стадия	Лист	Листов
РП	68	105

Шкафы. Монтажная схема

М 1:25

Кырлан Александр Сергеевич

выпуск 04.11.2026 № 8be4ef4c81 · стр. 76 из 117

Ведомости изделий, техники и фурнитуры

встроенная мебель и кухонный гарнитур · размеры в мм

Ведомость изделий

Марка	Наименование	Пом.	Ш×Г×В, мм	Корпус	Фасад	Кромка, мм	Кол.
М5**	Шкаф-купе	4	1600×600×2450	ЛДСП 16	МДФ, шпон / эмаль 18 мм; вставка зеркало серебро 4 мм на безопасной плёнке, в профиле двери	0,4 / 1	1
М7**	Пенал: холодильник встр.	5	600×650×2200	ЛДСП 16	МДФ: шпон американского ореха (нижние модули) и эмаль пыльно-синяя с узкой филёнкой (колонны), латунные ручки-скобы 18 мм	0,4 / 1	1
М8	Модуль нижний: ящики	5	350×600×900	ЛДСП 16	МДФ: шпон американского ореха (нижние модули) и эмаль пыльно-синяя с узкой филёнкой (колонны), латунные ручки-скобы 18 мм	0,4 / 1	1
М13	Модуль навесной: полки	5	350×350×900	ЛДСП 16	МДФ, эмаль пыльно-синяя, филёнка, латунные ручки 18 мм	0,4 / 1	1
М9	Модуль нижний: духовой шкаф, варочная	5	600×600×900	ЛДСП 16	МДФ: шпон американского ореха (нижние модули) и эмаль пыльно-синяя с узкой филёнкой (колонны), латунные ручки-скобы 18 мм	0,4 / 1	1
М14	Модуль навесной: полки	5	600×350×800	ЛДСП 16	МДФ, эмаль пыльно-синяя, филёнка, латунные ручки 18 мм	0,4 / 1	1
М10	Модуль нижний: ящики	5	600×600×900	ЛДСП 16	МДФ: шпон американского ореха (нижние модули) и эмаль пыльно-синяя с узкой филёнкой (колонны), латунные ручки-скобы 18 мм	0,4 / 1	1
М15	Модуль навесной: полки	5	600×350×900	ЛДСП 16	МДФ, эмаль пыльно-синяя, филёнка, латунные ручки 18 мм	0,4 / 1	1
М11**	Модуль нижний: мойка	5	800×600×900	ЛДСП 16	МДФ: шпон американского ореха (нижние модули) и эмаль пыльно-синяя с узкой филёнкой (колонны), латунные ручки-скобы 18 мм	0,4 / 1	1
М16	Модуль навесной: сушка	5	800×350×900	ЛДСП 16	МДФ, эмаль пыльно-синяя, филёнка, латунные ручки 18 мм	0,4 / 1	1
М12	Модуль под ПММ 60: без корпуса, фасад на дверь машины	5	600×600×900	без корпуса	МДФ: шпон американского ореха (нижние модули) и эмаль пыльно-синяя с узкой филёнкой (колонны), латунные ручки-скобы 18 мм — на дверь машины (навеска из её комплекта), цоколь		1
М17	Модуль навесной: полки	5	600×350×900	ЛДСП 16	МДФ, эмаль пыльно-синяя, филёнка, латунные ручки 18 мм	0,4 / 1	1

Ведомость встраиваемой техники

Поз.	Прибор	Ниша, вырез, мм	Вентиляция	Питание	Схема
М7**	Холодильник встраиваемый, ниша 1780	ниша 1780 × 560 × 550	решётка в цоколе, канал за корпусом, выход сверху	Р7**: М7**, Н=2050 — над нишей холодильника, съёмная панель	по модели
М9	Духовой шкаф встраиваемый, 60 см	ниша 560 × 600, глубина ≥ 550	зазор за шкафом, вырез в задней стенке	ЭВ2: М9, Н=150 — под духовым шкафом, доступ через ящик	по модели
М9	Варочная панель индукционная, 60 см	вырез в столешнице 560 × 490		ЭВ1: М8, Н=600 — в соседнем модуле, за ящиком	по модели
М11**	Мойка врезная / подстольная с сифоном	вырез по шаблону, ориентир 700 × 480		смеситель — выводы ВК	по модели
М12	Посудомоечная машина встраиваемая, 60 см	ниша 600 × 862 (от пола до низа столешницы)	зазор в цоколе, по схеме	Р6: М12, Н=300 — за ПММ — перенести в соседний модуль	по модели

Ведомость фурнитуры

№	Фурнитура	Тип, размер	Изделия	Кол.
1	Система дверей купе: профиль, направляющие, ролики	на 2 двери	М5**	1
2	Ручка-профиль вертикальная	в цвет профиля	М5**	2
3	Полкодержатель с фиксацией	ø5 мм	М5**, М7**, М13, М14, М15, М17	40
4	Штанга овальная 30×15, L = 776	+ 2 держателя	М5**	1
5	Полка для обуви выдвижная наклонная	ширина 776	М5**	3
6	Опора регулируемая с цоколем на клипсах	ход 20 мм	М5**	6
7	Анкер по основанию стены	по таблице крепежа	М5**, М13, М14, М15, М16, М17	15
8	Уголок крепления к стене от опрокидывания	стальной	М5**, М7**	4
9	Петля накладная 110° с доводчиком	чашка 35 мм	М7**, М13, М14, М15, М11**, М16, М17	29
10	Ручка-профиль	латунь матовая	М7**, М8, М13, М9, М14, М10, М15, М11**, М16, М12, М17	22
11	Опора кухонная регулируемая 100–120 мм	+ клипса цоколя	М7**, М8, М9, М10, М11**	22
12	Направляющие полного выдвижения с доводчиком NL 500	пара	М8, М9, М10	7
13	Навес регулируемый для навесного шкафа	пара на секцию	М13, М14, М15, М16, М17	5
14	Шина монтажная	L = 290	М13	1
15	Шина монтажная	L = 540	М14, М15, М17	3
16	Сушка для посуды в шкаф	ширина 800	М16	1
17	Шина монтажная	L = 740	М16	1
18	Комплект навески фасада ПММ	из поставки машины	М12	1

Примечания

1. Модели техники выбирает заказчик до изготовления мебели; ниши, вырезы и вентиляция — по монтажной схеме выбранной модели (условие гарантии), её номер вносится в ведомость.
2. Количество фурнитуры — по чертежам изделий; запас крепежа 5 %. Аналоги — по характеристикам (доводчик, нагрузка, ход).
3. Цвет корпусов, фасадов и профилей — по колерной карте проекта. Кромка — скрытые / видимые торцы, мм.

Допущения и предложения на листе

Основа листа: планировка по обводу плана заказчика, не замерена (К-1); высота до плиты 2650 мм от чистого пола — решение автора (ИЗ-1); отметки плана потолков сдвинуты на -95 мм (+2.745 плана = низ плиты), не замерено (К-2); толщины стен приняты: наружные 260 мм, перегородки 130 мм (К-1); положение стен и проёмов — по брифу без обмера и плана БТИ (К-1); разрешённая мощность 10 кВт принята, ТУ не переданы (К-6); вентканалы приняты, в брифе не заданы (К-5); тип дома, перекрытие и несущие стены не известны — документов нет (К-3); плита электрическая — принята, в брифе не указано (К-6); система заземления TN-C-S принята, ТУ не переданы (К-6); число жильцов 2 принято, в брифе не указано (К-9); подрайон климата не задан — принят не северный (жилые от 2,5 м) (К-26).

Знак «**» — предложение проектировщика, заказчиком не утверждено (согласовать с заказчиком): Р7 — высота 2050 мм выше нормы 1 м (ПУЭ 6.6.30) по назначению: розетка встроенного прибора — в колонне М7 над нишей, в антресоли за съёмной панелью; К-7: М5, М7, М11.

См. лист открытых вопросов (лист 5, записи К-1, К-3, К-5–К-7, К-9; лист 6, запись К-26).

Изм.	Кол.уч	Лист	№ док.	Подп.	Дата
Разраб.		Кырлан А.С.			04.11.26
Пров.					
ГИП					
Н. контр.					
Утв.					

ГД-2026-020-АИ

Квартира 68 м², элитный модерн

Общая площадь 68,47* м² · * размеры приняты, не замерены (реестр — л. 5–7, К-1)

Дизайн-проект интерьера

Стадия	Лист	Листов
РП	69	105

Ведомости изделий, техники и фурнитуры

М б/м

Кырлан Александр Сергеевич

выпуск 04.11.2026 № 8be4ef4c81 · стр. 77 из 117

09

Развёртки и узлы



Кырлан Александр Сергеевич

выпуск 04.11.2026 № 8be4ef4c81 · стр. 78 из 117

Реестр марок отделки и позиций альбома

Реестр марок отделки (О ↔ позиции колерной карты) и марки позиций по видам

Реестр марок отделки альбома

Марка	Поверхность	Материал, изделие	Цвет, код	Помещения	Колер. карта
О1	стены	окраска, Farrow & Ball Modern Emulsion, матовая, подготовка Q3	Farrow & Ball No. 2003 «Pointing»	1, 4, 5, 6, 7	К1
О2	акцентная стена	окраска, Tikkurila Euro Power 7, колеровка по NCS, матовая, подготовка Q3	Farrow & Ball No. 30 «Hague Blue — глубокий сине-зелёный»	1	К2
О3	плинтус	плинтус МДФ, h 80 мм, аналог: плинтус МДФ под покраску 80×16	Farrow & Ball No. 2003 «Pointing»	1, 4, 5, 6, 7	К4
О4	потолок	окраска, Tikkurila Euro Power 7, глубокоматовая, подготовка Q3	Tikkurila G503 «Calla»	1, 2, 3, 4, 5, 6, 7	К3, К5
О5	пол	инженерная доска, аналог: инженерная доска, дуб натуральный, масло, 1-полосная, 14/4 мм		1, 5, 6, 7	КМ1
О6	стены	облицовка плиткой, 600×1200×9 мм, аналог: керамогранит под травертин, матовый, затирка CG2WA		2, 3	КМ2
О7	пол	керамогранит, 600×600×9 мм, аналог: керамогранит ректифицированный под травертин, матовый, затирка CG2WA		2, 3	КМ3
О8	пол	керамогранит, 600×1200×9 мм, аналог: керамогранит ректифицированный под травертин, матовый, затирка CG2WA		4	КМ4
О9	фартук	керамогранит, 1200×600×9 мм, аналог: керамогранит под травертин, матовый, затирка CG2WA		5	КМ5
О10	акцентная стена	окраска, Tikkurila Euro Power 7, колеровка по NCS, матовая, подготовка Q3	Farrow & Ball No. 281 «Stiffkey Blue чернильный синий»	5	К6
О11	акцентная стена	окраска, Farrow & Ball Modern Emulsion, матовая, подготовка Q3	Farrow & Ball No. 43 «Eating Room Red брусничный красный»	6	К7
О12	акцентная стена	окраска, Farrow & Ball Modern Emulsion, матовая, подготовка Q3	Farrow & Ball No. 34 «Calke Green традиционный шалфей»	7	К8

Марки позиций альбома по видам

Префикс	Что обозначает, позиции	Листы
Д	двери: Д-1–Д-7	15–17
ОК	окна: ОК-1–ОК-3	15–17
М	мебель и оборудование: М1**, М3, М5**, М6**, М7**, М8–М10, М11**, М12–М17, М18**, М19**, М20**, М23**, М24**, М25, М26	18–22
П	сантехнические приборы: П1, П2, П3**, П4, П5**, П7, П9**, П10**, П16**	34–43
ДК	декор (картины, зеркала, растения): ДК1–ДК3, ДК4**, ДК5**, ДК6, ДК7**, ДК8–ДК10	1, 58–63
Т	текстиль (шторы, ковры): Т1**, Т2**, Т3, Т4**, Т5**, Т6**, Т7**, Т8**, Т9**, Т10**, Т11**, Т12**, Т13**, Т14**, Т15**	1, 58–63
Р	розетки: Р1–Р6, Р7**, Р8–Р27, Р29–Р45	23–31
LAN	розетки компьютерные: LAN1, LAN2	23–31
S	выключатели: S1–S10, S11**	23–31

Допущения и предложения на листе. Знак «*» принято (замерить). Знак «**» предложено (согласовать): пол пом. 1–7, плинтус пом. 1, 4–7, акцент пом. 1, 5–7, стены пом. 2, 3, фартук пом. 5. См. лист открытых вопросов (листы 5–7).

Марки позиций альбома по видам (продолжение)

Префикс	Что обозначает, позиции	Листы
ИП	извещатели: ИП1–ИП5	23–31
ЭВ	выводы кабеля: ЭВ1–ЭВ3, ЭВ4**, ЭВ5**, ЭВ6, ЭВ8, ЭВ9**, ЭВ10**, ЭВ11**, ЭВ12**, ЭВ13**, ЭВ14**	23–31
Св	светильники: Св1**, Св2**, Св3**, Св4**, Св5**, Св6**, Св7**, Св10**, Св11**, Св12**, Св13**, Св14**, Св15**, Св16**, Св17**, Св18, Св19**, Св26**, Св27**, Св28**, Св29**, Св30**, Св31**, Св36**, Св37**, Св38**, Св39**, Св40**, Св41**, Св42**, Св43**, Св44**, Св46**, Св47**, Св48**, Св49**, Св50**, Св51**, Св52**, Св53**, Св54**, Св55**, Св56**, Св57**, Св58**, Св59**	23–31
ДП, КУП, ТР	электроустановочные изделия: ДП1**, ДП2**, ДП3**, ДП4**, ДП5**, ДП6**, ДП7, КУП1**, КУП2**, ТР1**, ТР2**	23–31
ЩК, ЩС**	щиты: ЩК, ЩС**	23–31
ДФ	домофон: ДФ1	23–31
АР	точки доступа Wi-Fi: АР1**	23–31
ТВ	розетки ТВ: ТВ1	23–31
Ст В1, Ст К1, Ст Т3	стояки (системы В1, Т3, К1): Ст В1-2*, Ст К1-1*, Ст Т3-3*	34–43
О	марки отделки (реестр альбома): О1–О12	2–4, 70–98
К, КМ	позиции колерной карты: К1–К8, КМ1–КМ5	56, 57
РО	радиаторы отопления: РО-1**, РО-2**, РО-3**, РО-4**	32, 33

Примечания

1. Марка отделки О — одна на весь альбом: одна и та же отделка (материал, изделие, цвет, формат) на всех листах имеет одну марку; на развёртках и планах стоят марки этого реестра.
2. Столбец «Колер. карта» — позиции колерной карты (лист 56): К — окраска по коду цвета, КМ — материал без кода цвета; «Помещения» — номера по экспликации; количества — по ведомости отделки помещений (лист 54).
3. Марки позиций: один префикс — один вид позиций на весь альбом (двери Д, окна ОК, мебель М, сантехприборы П, декор ДК, текстиль Т, колерная карта К и КМ, радиаторы РО, розетки Р, выключатели S, светильники Св; стояки — «Ст» и система, например «Ст К1-1*»). Совпадение префиксов у разных видов — замечание к исходным данным, при выпуске исправляется в модели.

Изм.	Кол.уч	Лист	№ док.	Подп.	Дата
Разраб.		Кырлан А.С.			04.11.26
Пров.					
ГИП					
Н. контр.					
Утв.					

ГД-2026-020-АИ

Квартира 68 м², элитный модерн

Общая площадь 68,47* м² · * размеры приняты, не замерены (реестр — л. 5–7, К-1)

Дизайн-проект интерьера

Стадия	Лист	Листов
РП	70	105

Реестр марок отделки и позиций альбома

М б/м

Кырлан Александр Сергеевич

выпуск 04.11.2026 № 8be4ef4c81 · стр. 79 из 117

Схема расположения развёрток и узлов

План квартиры: марки развёрток по помещениям, выноски узлов, ведомость «марка → лист»

ПРЕДВАРИТЕЛЬНО · не для производства работ · открыто пунктов: 25 (реестр — л. 5–7)



Развёртки и узлы: марка → лист

Марка	Помещение / узел	Лист
А, Б	Кабинет (пом. 1)	72, 73
В	Кабинет (пом. 1)	74
Г	Кабинет (пом. 1)	75
А, Б, В	Санузел (пом. 2)	76
Г	Санузел (пом. 2)	77, 78
А, Б	Ванная (пом. 3)	79
В, Г	Ванная (пом. 3)	80, 81
А	Прихожая (пом. 4)	82
Б, В	Прихожая (пом. 4)	83
Г	Прихожая (пом. 4)	84, 85
А1	Кухня-столовая (пом. 5)	86, 87
А2, Б1, Б2	Кухня-столовая (пом. 5)	88
В, Г	Кухня-столовая (пом. 5)	89
А, Б	Гостиная (пом. 6)	90, 91
В, Г	Гостиная (пом. 6)	92
А1, А2	Спальня (пом. 7)	93
Б	Спальня (пом. 7)	94
В	Спальня (пом. 7)	95, 96
Г	Спальня (пом. 7)	97
узел 1	Порог 15 мм: мокрая зона — смежное помещение	98
узел 2	Короб стояков К1-1 с люком и звукоизоляцией	98
узел 3	Гидроизоляция санузла: заход на стены 200 мм, примыкание ванны	98
узел 4	Плинтус МДФ 80×16 мм у окрашенной стены по доске (ламинату)	98
узел 5	Плинтус МДФ 80×16 мм у окрашенной стены по керамограниту (плитке)	98

Условные обозначения

- А — марка развёртки: буква стены, стрелка — взгляд
- выноска узла: над полкой — узел, под полкой — лист
- 1 — номер помещения, площадь м²

Примечания

1. Развёртки — вид на стену изнутри помещения; буквы стен — одна система на весь альбом (как на листах выводов, плитки и отделки).
2. Стены без электроточек, мебели, декора и акцентной отделки развёрток не имеют: их отделка — по ведомости отделки помещений.
3. Узлы — на листе узлов; места применения — по выноскам этого листа и ведомости «марка → лист».

Допущения и предложения на листе. Знак «*» принято (замерить): Ст К1-1, Ст В1-2, Ст Т3-3. Знак «**» предложено (согласовать). См. лист открытых вопросов (листы 5–7).

1000 мм · печать 1:1

Изм.	Кол.уч	Лист	№ док.	Подп.	Дата
Разраб.		Кырлан А.С.			04.11.26
Пров.					
ГИП					
Н. контр.					
Утв.					

ГД-2026-020-АИ

Квартира 68 м², элитный модерн

Общая площадь 68,47* м² · * размеры приняты, не замерены (реестр — л. 5–7, К-1)

Дизайн-проект интерьера

Стадия	Лист	Листов
РП	71	105

Схема расположения развёрток и узлов

М 1:50

Кырлан Александр Сергеевич


выпуск 04.11.2026 № 8be4ef4c81 · стр. 80 из 117

Развёртки стен А, Б. Кабинет (пом. 1)

Кабинет (пом. 1) · вид изнутри помещения · размеры в мм, отметки в м


ПРЕДВАРИТЕЛЬНО · не для производства работ · открыто пунктов: 25 (реестр — л. 5–7)

Развёртка стены А

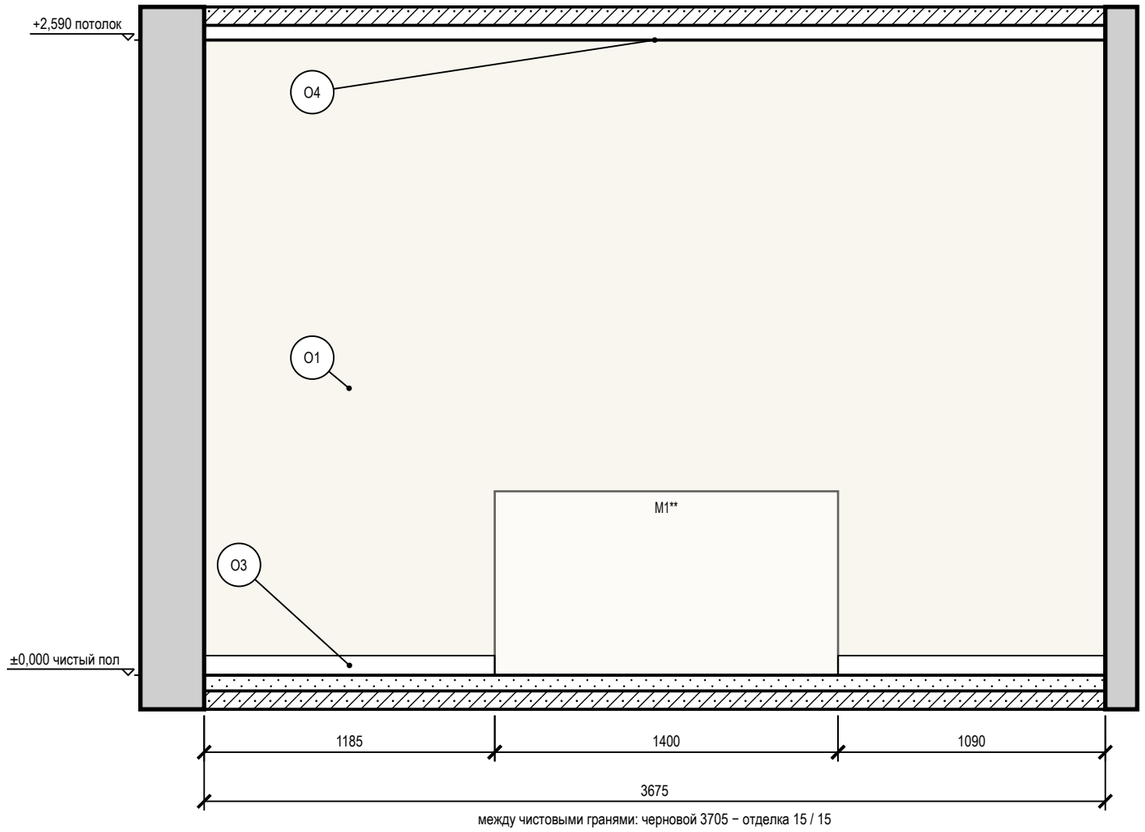


между чистовыми гранями: черновой 3705 − отделка 15 / 15

Развёртка стены Б

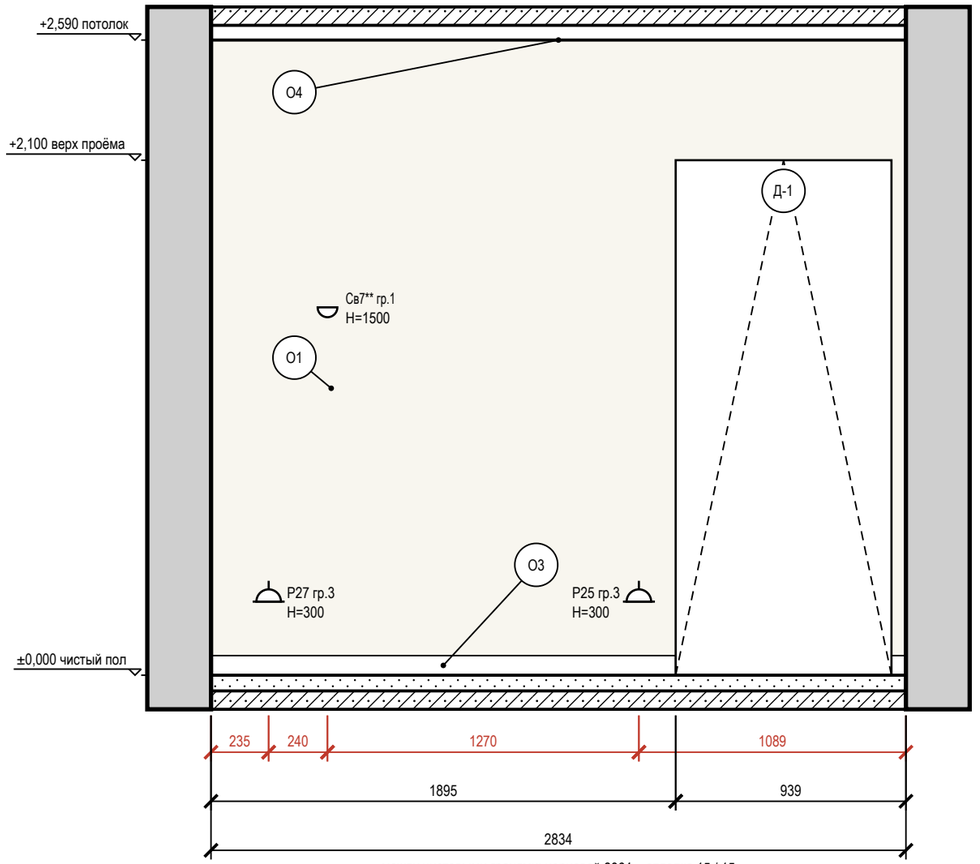

между чистовыми гранями: черновой 2864 − отделка 15 / 15

Схема развёрток (М 1:100)

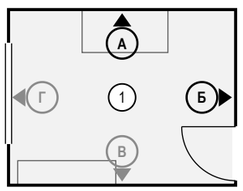

Условные обозначения

- розетка с заземляющим контактом; у знака — марка, ×N постов в рамке, гр. — группа щита, Н — высота оси, мм
- светильник настенный (бра), Н — высота оси
- привязки точек и выводов от угла и от пола, мм
- мебель и приборы — фасад по расстановке (условно)
- дверной проём; марка двери — в кружке
- стены и перекрытия в сечении
- окраска: тон — цвет по коду производителя (условно)
- О1 — марка отделки по реестру отделки альбома
- А — марка развёртки: буква стены, стрелка — взгляд

Ведомость отделки (на листе)

Марка	Поверхность	Материал, изделие	Цвет, код	Кол.
О1	стены	окраска, Farrow & Ball Modern Emulsion, матовая, подготовка Q3	Farrow & Ball No. 2003 «Pointing»	15 м²
О3	плинтус	плинтус МДФ, h 80 мм, аналог: плинтус МДФ под покраску 80×16	Farrow & Ball No. 2003 «Pointing»	4,2 м
О4	потолок	окраска, Tikkurila Euro Power 7, глубокоматовая, подготовка Q3	Tikkurila G503 «Calla»	10,6 м²

Примечания

1. Развёртки — вид на стену изнутри помещения, по часовой стрелке; расположение — на схеме листа и на листе 71; размеры — в мм по чистовым поверхностям; отметки — в м от ±0,000; высоты Н — от чистого пола помещения до оси изделия, у декора — до центра.
2. Красная цепочка — привязки электроточек и выводов по осям от угла чистовых стен; высота Н — у знака, от чистого пола до оси; высоты мебели, проёмов и границ отделки — колонкой отметок слева. Стена с 5 и более точками или с мелкими звеньями привязок показана двумя видами: архитектурная развёртка (мебель, отделка, проёмы, высоты) и вид «Привязки» на отдельном листе — точки и выводы с марками, одна цепочка по осям и таблица привязок (каждая точка — строка).
3. Стена А показана двумя видами: здесь — архитектурная развёртка (мебель, отделка, проёмы, высоты), электроточки и выводы ВК с привязками и таблицей — на листе 73 («Привязки»).
4. У знака электроточки: марка (Р — розетка, S — выключатель, Св — светильник, ЭВ — вывод кабеля), ×N — число постов в рамке, гр. — группа щита, Н — высота оси от чистого пола, мм; группы по клавишам выключателя — на листе выключателей.
5. Схема мебели, приборов и декора не является технической документацией для производства мебели; габариты — по паспортам изделий.

1000 мм · печать 1:1

Допущения и предложения на листе. Знак «*» принято (замерить): окно пом. 1 (стена Г), дверь пом. 1 (стена Б). Знак «**» предложено (согласовать). См. лист открытых вопросов (листы 5–7).

Изм.	Кол.уч	Лист	№ док.	Подп.	Дата
Разраб.		Кырлан А.С.			04.11.26
Пров.					
ГИП					
Н. контр.					
Утв.					

ГД-2026-020-АИ

Квартира 68 м², элитный модерн

Общая площадь 68,47* м² · * размеры приняты, не замерены (реестр — л. 5–7, К-1)

Дизайн-проект интерьера

Стадия	Лист	Листов
РП	72	105

Развёртки стен А, Б. Кабинет (пом. 1)

М 1:25

Кырлан Александр Сергеевич

выпуск 04.11.2026 № 8be4ef4c81 · стр. 81 из 117

Привязки электроточек, стена А. Кабинет (пом. 1)

Кабинет (пом. 1) · вид изнутри помещения · привязки в мм, отметки в м · к развёртке на листе 72

ПРЕДВАРИТЕЛЬНО · не для производства работ · открыто пунктов: 25 (реестр — л. 5–7)

Развёртка стены А: электроточки и выводы

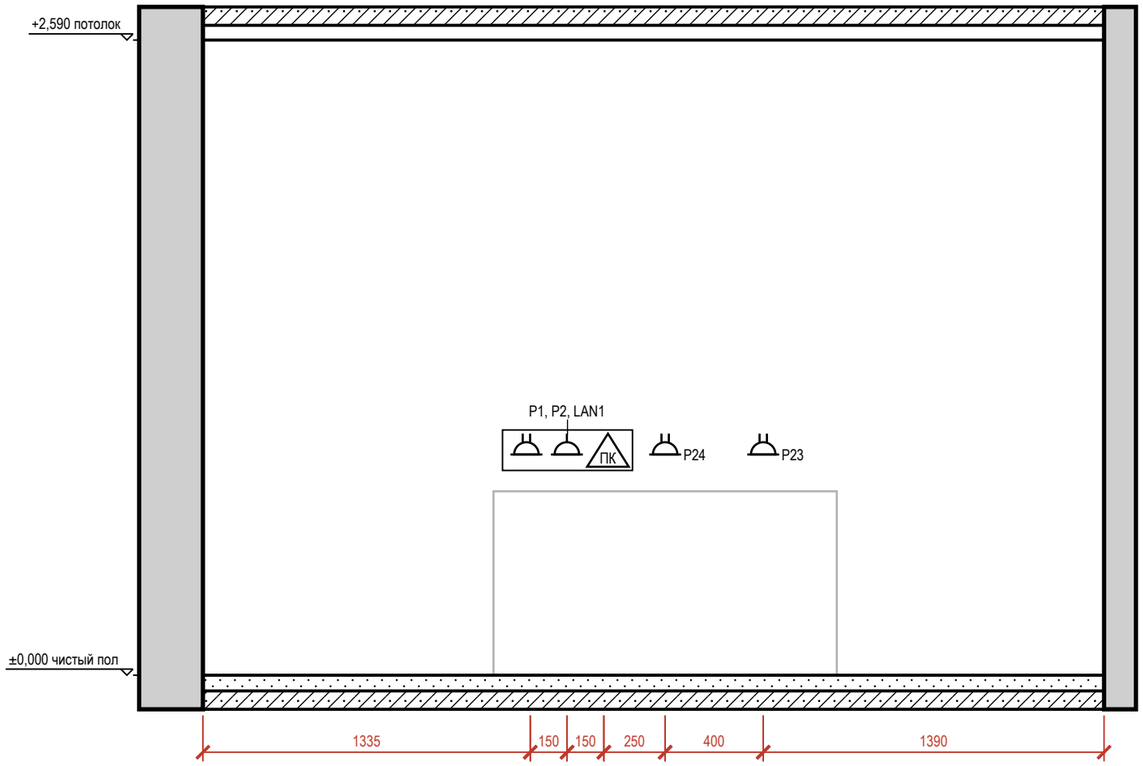


Таблица привязок электроточек и выводов

Марка	Назначение	От угла, мм	H от пола, мм	Примечание
P1	розетка: рабочий стол	1335	900	рамка 2 поста, гр. 3
P2	розетка: рабочий стол: монитор	1485	900	гр. 3
LAN1	розетка RJ45: рабочий стол	1635	900	
P24	розетка: рабочий стол: компьютер, монитор, зарядки	1885	900	рамка 2 поста, гр. 3
P23	розетка: рабочий стол: компьютер, монитор, зарядки	2285	900	рамка 2 поста, гр. 3

Условные обозначения

- розетка с заземляющим контактом; у знака — марка, ×N постов в рамке, гр. — группа щита, H — высота оси, мм
- ПК — розетка компьютерная RJ45
- привязки точек и выводов от угла и от пола, мм
- A — марка развёртки: буква стены, стрелка — взгляд

Схема развёрток (М 1:50)

Примечания

1. Вид «Привязки» стены А — электроточки и выводы ВК; архитектурная развёртка (мебель, отделка, проёмы, высоты) — на листе 72, расположение — на листе 71. Мебель и приборы — подложкой для ориентира; их марки и обозначения мебели, проёмов и стен — там же.
2. Привязки — в мм: по горизонтали от левого чистового угла стены до оси изделия, H — от чистого пола до оси; все точки — в таблице привязок. Красная цепочка — привязки по осям; точки ближе 150 мм одна к другой в цепочку не дробятся — их привязки только в таблице.
3. У знака — марка электроточки (Р — розетка, S — выключатель, Св — светильник, ЭВ — вывод кабеля); посты в рамке и группа щита — в графе «Примечание»; группы по клавишам выключателя — на листе выключателей.

Допущения и предложения на листе

Основа листа: планировка по обводу плана заказчика, не замерена (К-1); высота до плиты 2650 мм от чистого пола — решение автора (ИЗ-1); отметки плана потолков сдвинуты на -95 мм (+2.745 плана = низ плиты), не замерено (К-2); толщины стен приняты: наружные 260 мм, перегородки 130 мм (К-1); положение стен и проёмов — по брифу без обмера и плана БТИ (К-1); разрешённая мощность 10 кВт принята, ТУ не переданы (К-6); вентканалы приняты, в брифе не заданы (К-5); тип дома, перекрытие и несущие стены не известны — документов нет (К-3); плита электрическая — принята, в брифе не указано (К-6); система заземления TN-C-S принята, ТУ не переданы (К-6); число жильцов 2 принято, в брифе не указано (К-9); подрайон климата не задан — принят не северный (жилые от 2,5 м) (К-26).

Знак «*» — принято, не замерено и не подтверждено (замерить на объекте): К-1: окно пом. 1 (стена Г) — окно: положение, ширина, высота и подоконник приняты по обводу плана заказчика, без обмера, не замерены; дверь пом. 1 (стена Б) — проём принят по обводу плана заказчика, без обмера: положение и ширина сняты с плана, не замерены.

См. лист открытых вопросов (лист 5, записи К-1, К-3, К-5, К-6, К-9; лист 6, запись К-26).

1000 мм · печать 1:1

Изм.	Кол.уч	Лист	№ док.	Подп.	Дата
Разраб.		Кырлан А.С.			04.11.26
Пров.					
ГИП					
Н. контр.					
Утв.					

ГД-2026-020-АИ

Квартира 68 м², элитный модерн

Общая площадь 68,47* м² · * размеры приняты, не замерены (реестр — л. 5–7, К-1)

Дизайн-проект интерьера

Стадия	Лист	Листов
РП	73	105

Привязки электроточек, стена А. Кабинет (пом. 1)

М 1:25

Кырлан Александр Сергеевич


выпуск 04.11.2026 № 8be4ef4c81 · стр. 82 из 117

Развёртка стены В. Кабинет (пом. 1)

Кабинет (пом. 1) · вид изнутри помещения · размеры в мм, отметки в м


ПРЕДВАРИТЕЛЬНО · не для производства работ · открыто пунктов: 25 (реестр — л. 5–7)

Развёртка стены В

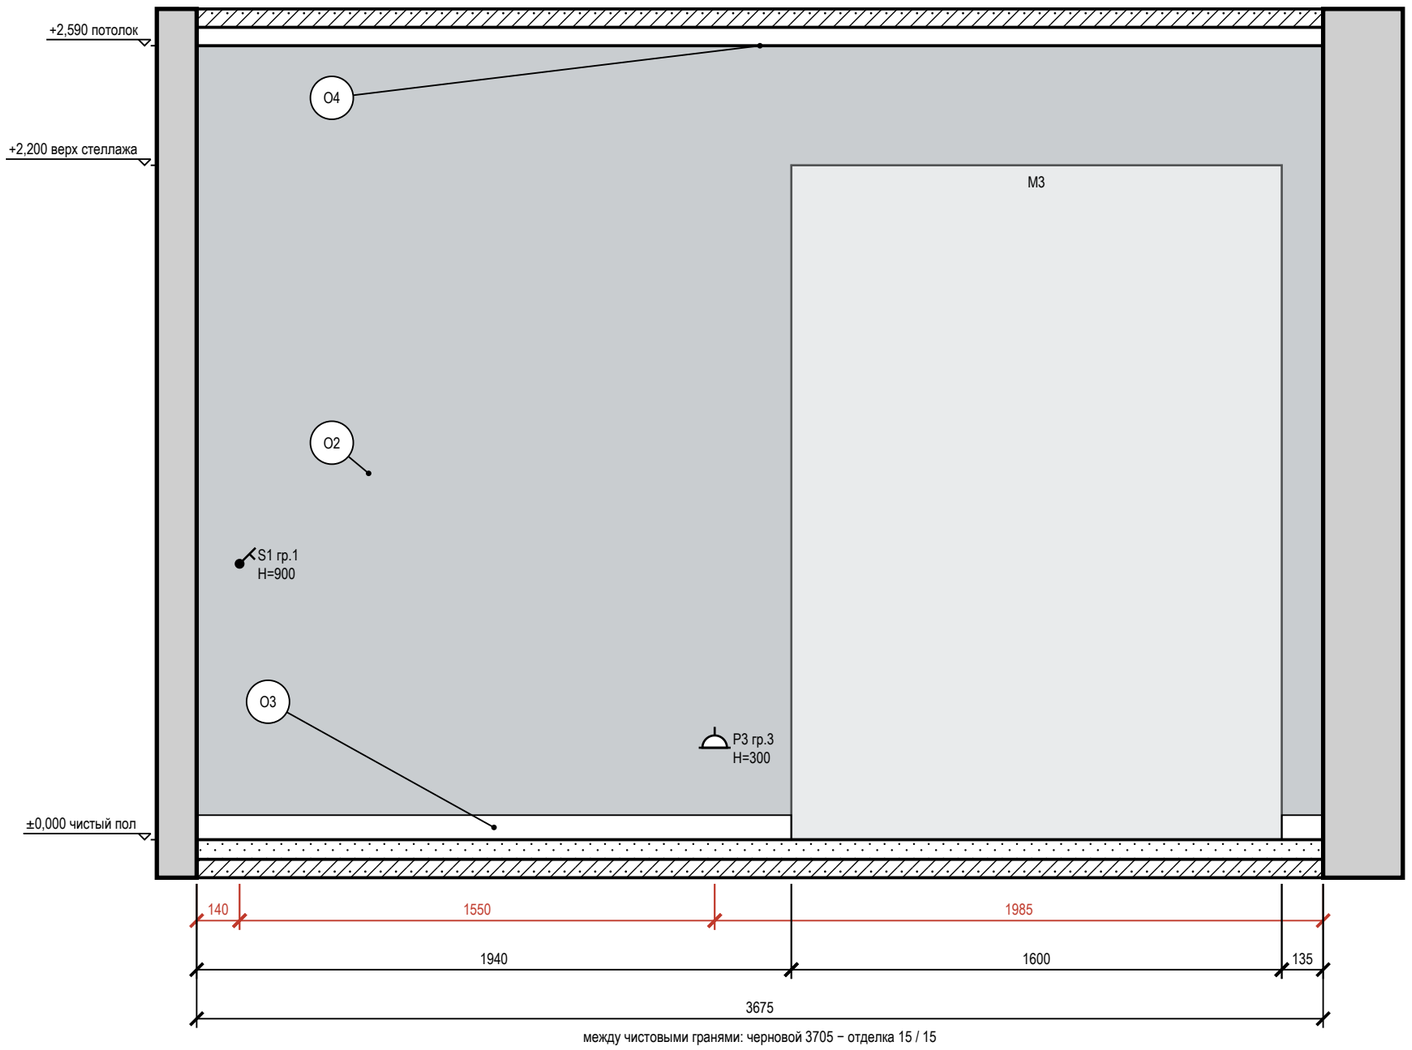

между чистовыми гранями: черновой 3705 − отделка 15 / 15

Схема развёрток (М 1:100)

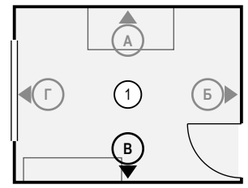

Условные обозначения

- розетка с заземляющим контактом; у знака — марка, ×N постов в рамке, гр. — группа щита, Н — высота оси, мм
- выключатель одноклавишный
- привязки точек и выводов от угла и от пола, мм
- мебель и приборы — фасад по расстановке (условно)
- стены и перекрытия в сечении
- окраска: тон — цвет по коду производителя (условно)
- О1 — марка отделки по реестру отделки альбома
- А — марка развёртки: буква стены, стрелка — взгляд

Ведомость отделки (на листе)

Марка	Поверхность	Материал, изделие	Цвет, код	Кол.
О2	акцентная стена	окраска, Tikkurila Euro Power 7, колеровка по NCS, матовая, подготовка Q3	Farrow & Ball No. 30 «Hague Blue глубокий сине-зелёный»	9,5 м²
О3	плинтус	плинтус МДФ, h 80 мм, аналог: плинтус МДФ под покраску 80×16	Farrow & Ball No. 2003 «Pointing»	2,1 м
О4	потолок	окраска, Tikkurila Euro Power 7, глубокоматовая, подготовка Q3	Tikkurila G503 «Calla»	10,6 м²

Допущения и предложения на листе

Основа листа: планировка по обводу плана заказчика, не замерена (К-1); высота до плиты 2650 мм от чистого пола — решение автора (ИЗ-1); отметки плана потолков сдвинуты на -95 мм (+2.745 плана = низ плиты), не замерено (К-2); толщины стен приняты: наружные 260 мм, перегородки 130 мм (К-1); положение стен и проёмов — по брифу без обмера и плана БТИ (К-1); разрешённая мощность 10 кВт принята, ТУ не переданы (К-6); вентканалы приняты, в брифе не заданы (К-5); тип дома, перекрытие и несущие стены не известны — документов нет (К-3); плита электрическая — принята, в брифе не указано (К-6); система заземления TN-C-S принята, ТУ не переданы (К-6); число жильцов 2 принято, в брифе не указано (К-9); подрайон климата не задан — принят не северный (жилые от 2,5 м) (К-26).

Знак «*» — принято, не замерено и не подтверждено (замерить на объекте): К-1: окно пом. 1 (стена Г) — окно: положение, ширина, высота и подоконник приняты по обводу плана заказчика, без обмера, не замерены; дверь пом. 1 (стена Б) — проём принят по обводу плана заказчика, без обмера: положение и ширина сняты с плана, не замерены.

См. лист открытых вопросов (лист 5, записи К-1, К-3, К-5, К-6, К-9; лист 6, запись К-26).

Примечания

1. Развёртки — вид на стену изнутри помещения, по часовой стрелке; расположение — на схеме листа и на листе 71; размеры — в мм по чистовым поверхностям; отметки — в м от ±0,000; высоты Н — от чистого пола помещения до оси изделия, у декора — до центра.
2. Красная цепочка — привязки электроточек и выводов по осям от угла чистовых стен; высота Н — у знака, от чистого пола до оси; высоты мебели, проёмов и границ отделки — колонкой отметок слева. Стена с 5 и более точками или с мелкими звеньями привязок показана двумя видами: архитектурная развёртка (мебель, отделка, проёмы, высоты) и вид «Привязки» на отдельном листе — точки и выводы с марками, одна цепочка по осям и таблица привязок (каждая точка — строка).
3. У знака электроточки: марка (Р — розетка, S — выключатель, Св — светильник, ЭВ — вывод кабеля), ×N — число постов в рамке, гр. — группа щита, Н — высота оси от чистого пола, мм; группы по клавишам выключателя — на листе выключателей.
4. Схема мебели, приборов и декора не является технической документацией для производства мебели; габариты — по паспортам изделий.

1000 мм · печать 1:1

Изм.	Кол.уч	Лист	№ док.	Подп.	Дата
Разраб.		Кырлан А.С.			04.11.26
Пров.					
ГИП					
Н. контр.					
Утв.					

ГД-2026-020-АИ

Квартира 68 м², элитный модерн

Общая площадь 68,47* м² · * размеры приняты, не замерены (реестр — л. 5–7, К-1)

Дизайн-проект интерьера

Стадия	Лист	Листов
РП	74	105

Развёртка стены В. Кабинет (пом. 1)

М 1:20

Кырлан Александр Сергеевич


выпуск 04.11.2026 № 8be4ef4c81 · стр. 83 из 117

Развёртка стены Г. Кабинет (пом. 1)

Кабинет (пом. 1) · вид изнутри помещения · размеры в мм, отметки в м

ПРЕДВАРИТЕЛЬНО · не для производства работ · открыто пунктов: 25 (реестр — л. 5–7)

Развёртка стены Г

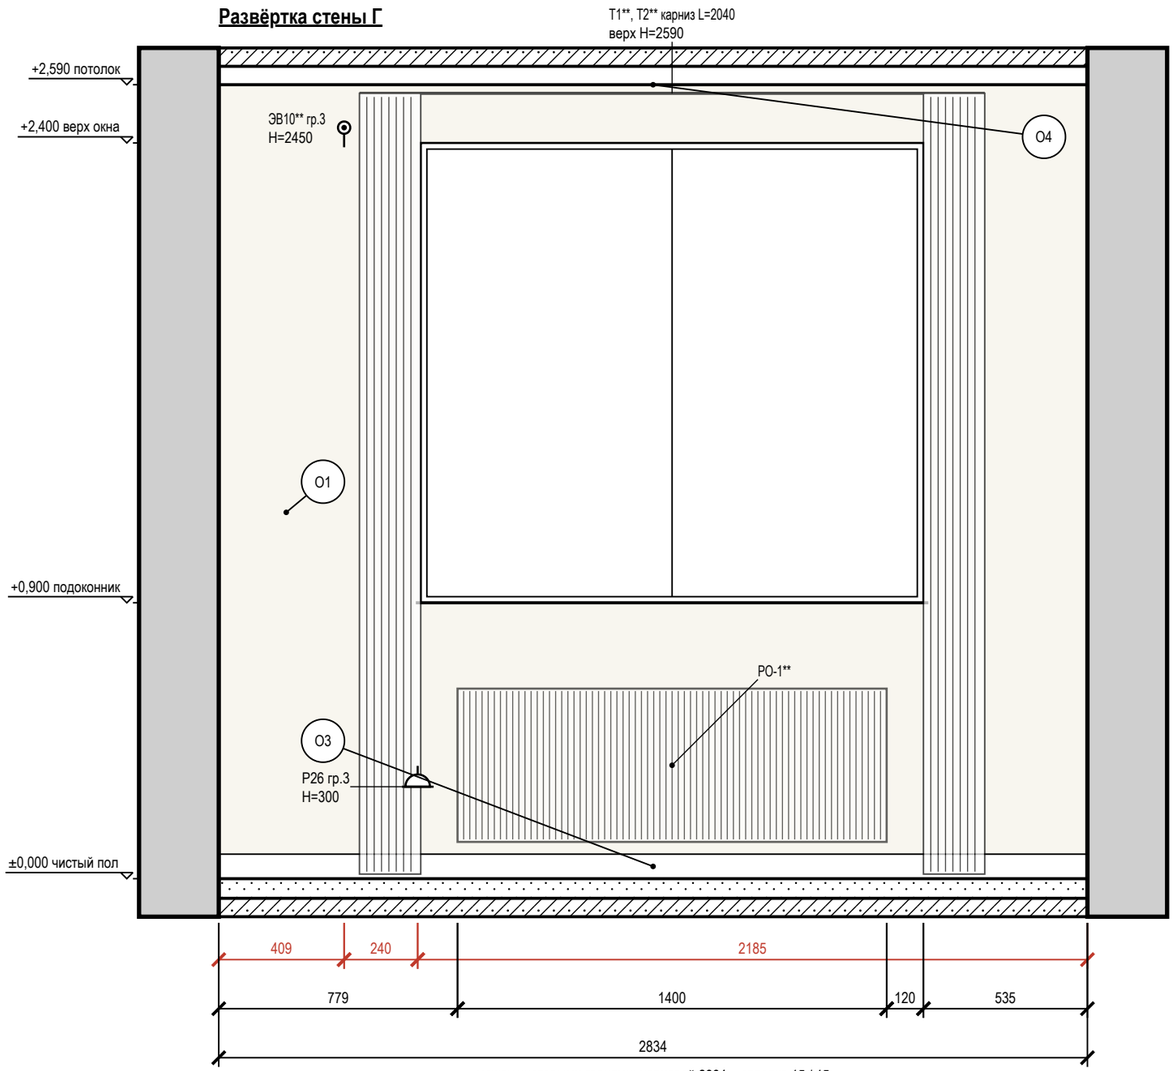

между чистовыми гранями: черновой 2864 − отделка 15 / 15


Допущения и предложения на листе. Основа листа: планировка по обводу плана заказчика, не замерена (К-1); высота до плиты 2650 мм от чистого пола — решение автора (ИЗ-1); отметки плана потолков сдвинуты на -95 мм (+2.745 плана = низ плиты), не замерено (К-2); толщины стен приняты: наружные 260 мм, перегородки 130 мм (К-1); положение стен и проёмов — по брифу без обмера и плана БТИ (К-1); разрешённая мощность 10 кВт принята, ТУ не переданы (К-6); вентканалы приняты, в брифе не заданы (К-5); тип дома, перекрытие и несущие стены не известны — документов нет (К-3); плита электрическая — принята, в брифе не указано (К-6); система заземления TN-C-S принята, ТУ не переданы (К-6); число жильцов 2 принято, в брифе не указано (К-9); подрайон климата не задан — принят не северный (жилые от 2,5 м) (К-26). Знак «*» — принято, не замерено и не подтверждено (замерить на объекте): К-1: окно пом. 1 (стена Г) — окно: положение, ширина, высота и подоконник приняты по обводу плана заказчика, без обмера, не замерены; дверь пом. 1 (стена Б) — проём принят по обводу плана заказчика, без обмера: положение и ширина сняты с плана, не замерены. Знак «**» — предложение проектировщика, заказчиком не утверждено (согласовать с заказчиком): РО-1 — подключение боковое, воздухоотводчик Маевского и термоголовка — типовое решение для панельного 22; тип подключения зависит от стояка и модели радиатора (запись реестра К-4: положение стояков); ЭВ10 — электропривод штор — предложение по умолчанию (комфорт): вывод у окна рядом с карнизом; без привода вывод остаётся резервным, заказчик может снять. См. лист открытых вопросов (лист 5, записи К-1, К-3, К-5–К-7, К-9; лист 6, запись К-26).

Примечания

1. Развёртки — вид на стену изнутри помещения, по часовой стрелке; расположение — на схеме листа и на листе 71; размеры — в мм по чистовым поверхностям; отметки — в м от ±0,000; высоты H — от чистого пола помещения до оси изделия, у декора — до центра.
2. Красная цепочка — привязки электроточек и выводов по осям от угла чистовых стен; высота H — у знака, от чистого пола до оси; высоты мебели, проёмов и границ отделки — колонкой отметок слева. Стена с 5 и более точками или с мелкими звеньями привязок показана двумя видами: архитектурная развёртка (мебель, отделка, проёмы, высоты) и вид «Привязки» на отдельном листе — точки и выводы с марками, одна цепочка по осям и таблица привязок (каждая точка — строка).
3. У знака электроточки: марка (Р — розетка, S — выключатель, Св — светильник, ЭВ — вывод кабеля), ×N — число постов в рамке, гр. — группа щита, H — высота оси от чистого пола, мм; группы по клавишам выключателя — на листе выключателей.
4. Схема мебели, приборов и декора не является технической документацией для производства мебели; габариты — по паспортам изделий.
5. Карнизы (шины) — по ведомости текстиля декоратора: длина L и верх H на развёртке — те же числа, что в ведомости; крепление — до окраски потолка.

1000 мм · печать 1:1

Схема развёрток (М 1:100)

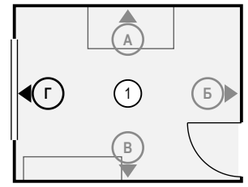

Условные обозначения

- розетка с заземляющим контактом; у знака — марка, ×N постов в рамке, гр. — группа щита, H — высота оси, мм
- вывод кабеля для подключения прибора (без розетки), марка ЭВ
- привязки точек и выводов от угла и от пола, мм
- мебель и приборы — фасад по расстановке (условно)
- карниз (шина) и шторы в собранном виде: марка T, длина L, верх H
- окно: проём, рама, подоконник
- радиатор отопления; марка — по плану отопления
- стены и перекрытия в сечении
- окраска: тон — цвет по коду производителя (условно)
- O1 — марка отделки по реестру отделки альбома
- A — марка развёртки: буква стены, стрелка — взгляд

Ведомость отделки (на листе)

Марка	Поверхность	Материал, изделие	Цвет, код	Кол.
O1	стены	окраска, Farrow & Ball Modern Emulsion, матовая, подготовка Q3	Farrow & Ball No. 2003 «Pointing»	4,9 м²
O3	плинтус	плинтус МДФ, h 80 мм, аналог: плинтус МДФ под покраску 80×16	Farrow & Ball No. 2003 «Pointing»	2,8 м
O4	потолок	окраска, Tikkurila Euro Power 7, глубокоматовая, подготовка Q3	Tikkurila G503 «Calla»	10,6 м²

Изм.	Кол.уч	Лист	№ док.	Подп.	Дата
Разраб.		Кырлан А.С.			04.11.26
Пров.					
ГИП					
Н. контр.					
Утв.					

ГД-2026-020-АИ

Квартира 68 м², элитный модерн

Общая площадь 68,47* м² · * размеры приняты, не замерены (реестр — л. 5–7, К-1)

Дизайн-проект интерьера

Стадия	Лист	Листов
РП	75	105

Развёртка стены Г. Кабинет (пом. 1)

М 1:20

Кырлан Александр Сергеевич


выпуск 04.11.2026 № 8be4ef4c81 · стр. 84 из 117

Развёртки стен А, Б, В. Санузел (пом. 2)

Санузел (пом. 2) · вид изнутри помещения · размеры в мм, отметки в м


ПРЕДВАРИТЕЛЬНО · не для производства работ · открыто пунктов: 25 (реестр — л. 5–7)

Развёртка стены А

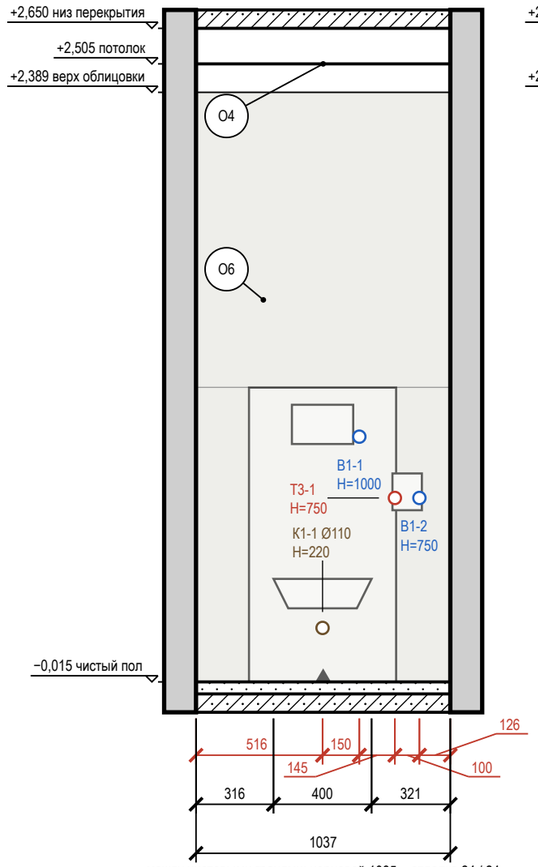


между чистовыми гранями: черновой 1085 − отделка 24 / 24

Развёртка стены Б

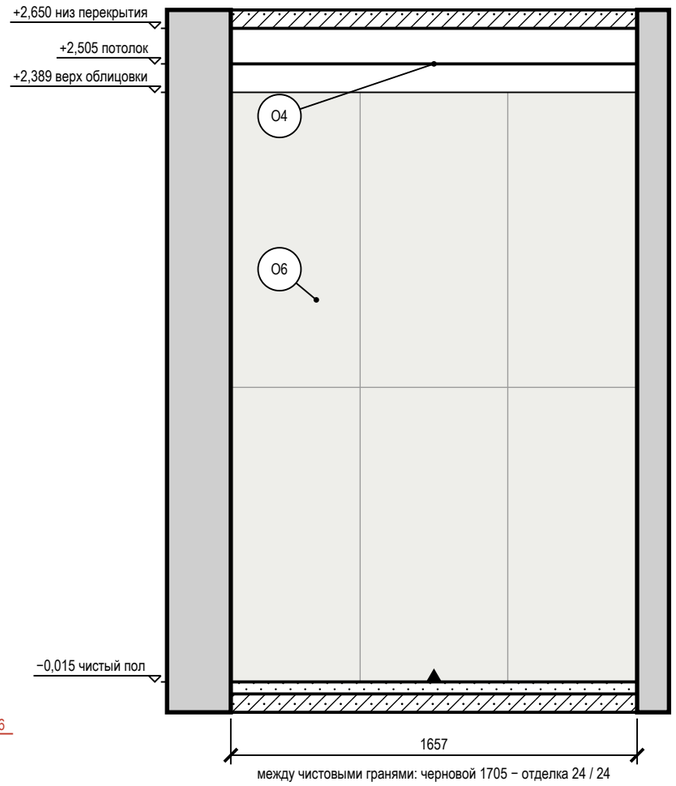

между чистовыми гранями: черновой 1705 − отделка 24 / 24

Развёртка стены В

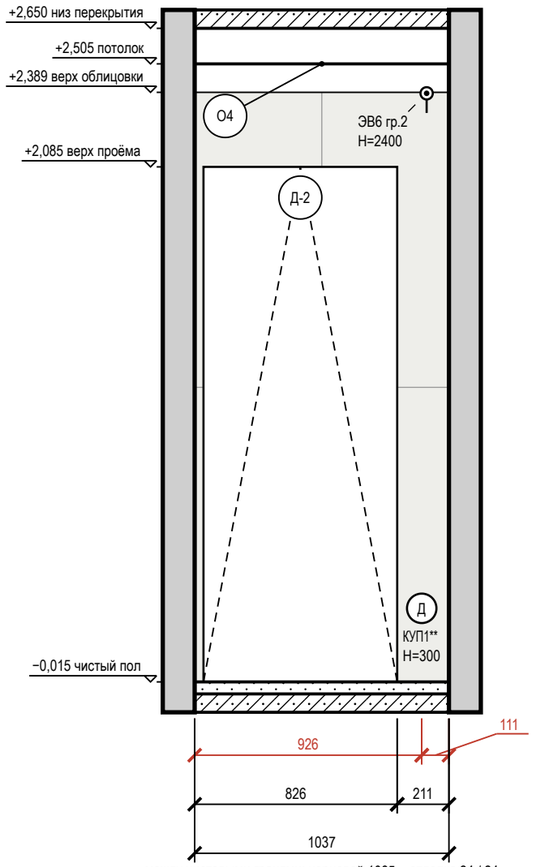


между чистовыми гранями: черновой 1085 − отделка 24 / 24

Условные обозначения

- вывод кабеля для подключения прибора (без розетки), марка ЭВ
- вывод В1 (код — в ведомости привязок)
- вывод Т3 (код — в ведомости привязок)
- вывод К1 (код — в ведомости привязок)
- привязки точек и выводов от угла и от пола, мм
- мебель и приборы — фасад по расстановке (условно)
- дверной проём; марка двери — в кружке
- стены и перекрытия в сечении
- плитка: сетка швов по формату, ▲ — ось старта
- О1 — марка отделки по реестру отделки альбома
- А — марка развёртки: буква стены, стрелка — взгляд

Схема развёрток (М 1:100)

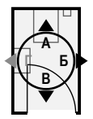

Ведомость отделки (на листе)

Марка	Поверхность	Материал, изделие	Цвет, код	Кол.
О4	потолок	окраска, Tikkurila Euro Power 7, матовая, подготовка Q3	Tikkurila G503 «Calla»	1,9 м²
О6	стены	облицовка плиткой, 600×1200×9 мм, аналог: керамогранит под травертин, матовый, затирка CG2WA		7,3 м²

Допущения и предложения на листе

Основа листа: планировка по обводу плана заказчика, не замерена (К-1); высота до плиты 2650 мм от чистого пола — решение автора (ИЗ-1); отметки плана потолков сдвинуты на -95 мм (+2.745 плана = низ плиты), не замерено (К-2); толщины стен приняты: наружные 260 мм, перегородки 130 мм (К-1); положение стен и проёмов — по брифу без обмера и плана БТИ (К-1); разрешённая мощность 10 кВт принята, ТУ не переданы (К-6); вентканалы приняты, в брифе не заданы (К-5); тип дома, перекрытие и несущие стены не известны — документов нет (К-3); плита электрическая — принята, в брифе не указано (К-6); система заземления TN-C-S принята, ТУ не переданы (К-6); число жильцов 2 принято, в брифе не указано (К-9); подрайон климата не задан — принят не северный (жилые от 2,5 м) (К-26).

Знак «**» — предложение проектировщика, заказчиком не утверждено (согласовать с заказчиком): КУП1 — коробка уравнивания потенциалов, проводник от шины РЕ; К-1: дверь пом. 2 (стена В) — проём принят по обводу плана заказчика, без обмера: положение и ширина сняты с плана, не замерены; открывание наружу (в прихожую): санузел 1,1 м — внутрь полотно задевает раковину П14.

См. лист открытых вопросов (лист 5, записи К-1, К-3, К-5, К-6, К-9; лист 6, запись К-26).

Примечания

1. Развёртки — вид на стену изнутри помещения, по часовой стрелке; расположение — на схеме листа и на листе 71; размеры — в мм по чистовым поверхностям; отметки — в м от ±0,000; высоты Н — от чистого пола помещения до оси изделия, у декора — до центра.
2. Красная цепочка — привязки электроточек и выводов по осям от угла чистовых стен; высота Н — у знака, от чистого пола до оси; высоты мебели, проёмов и границ отделки — колонкой отметок слева. Стена с 5 и более точками или с мелкими звеньями привязок показана двумя видами: архитектурная развёртка (мебель, отделка, проёмы, высоты) и вид «Привязки» на отдельном листе — точки и выводы с марками, одна цепочка по осям и таблица привязок (каждая точка — строка).
3. У знака электроточки: марка (Р — розетка, S — выключатель, Св — светильник, ЭВ — вывод кабеля), ×N — число постов в рамке, гр. — группа щита, Н — высота оси от чистого пола, мм; группы по клавишам выключателя — на листе выключателей.
4. Схема мебели, приборов и декора не является технической документацией для производства мебели; габариты — по паспортам изделий (* — высота не задана в проекте, показана по типовому изделию).
5. Облицовка — по сетке швов 2 мм, раскладка от оси стены (треугольник у пола), целые ряды от пола; подрезки — по листу раскладки плитки.
6. Гидроизоляция в 2 слоя, заход на стены 200 мм — до облицовки, с актом скрытых работ и тестом проливом (узел — на листе узлов).

1000 мм · печать 1:1

Изм.	Кол.уч	Лист	№ док.	Подп.	Дата
Разраб.		Кырлан А.С.			04.11.26
Пров.					
ГИП					
Н. контр.					
Утв.					

ГД-2026-020-АИ

Квартира 68 м², элитный модерн

Общая площадь 68,47* м² · * размеры приняты, не замерены (реестр — л. 5–7, К-1)

Дизайн-проект интерьера

Стадия	Лист	Листов
РП	76	105

Развёртки стен А, Б, В. Санузел (пом. 2)

М 1:25

Кырлан Александр Сергеевич

выпуск 04.11.2026 № 8be4ef4c81 · стр. 85 из 117

Развёртка стены Г. Санузел (пом. 2)

Санузел (пом. 2) · вид изнутри помещения · размеры в мм, отметки в м

ПРЕДВАРИТЕЛЬНО · не для производства работ · открыто пунктов: 25 (реестр — л. 5–7)

Развёртка стены Г


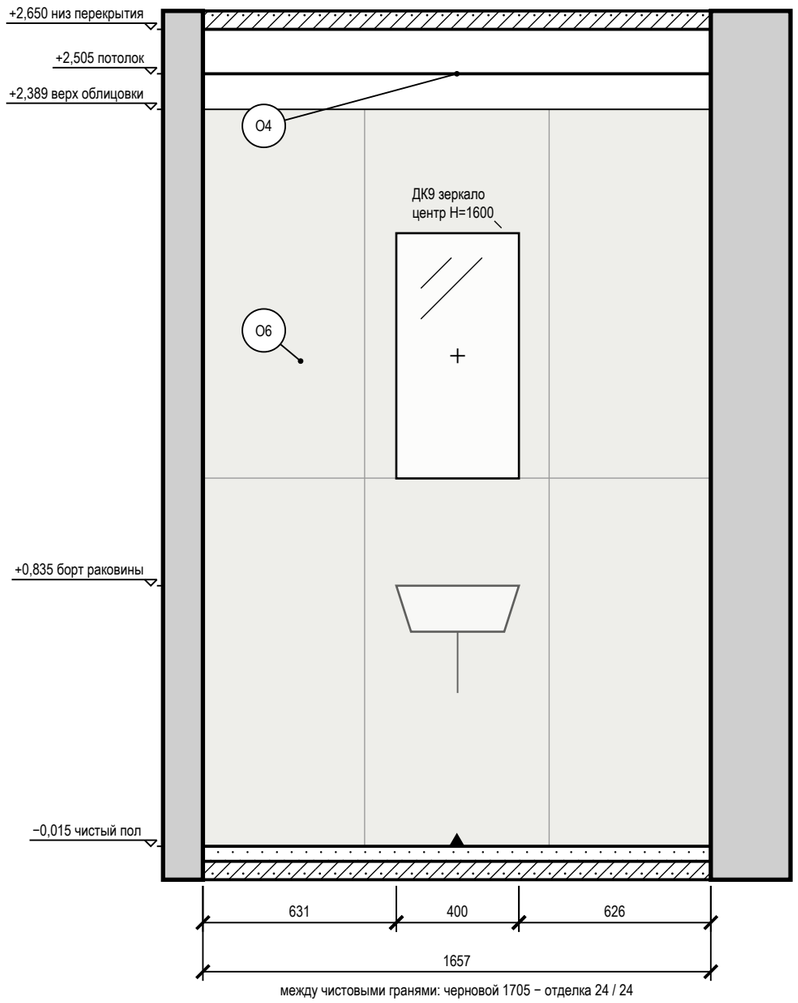


Схема развёрток (М 1:100)

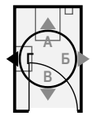

Условные обозначения

- мебель и приборы — фасад по расстановке (условно)
- зеркало: марка Д, крест — центр, Н — высота центра, мм
- стены и перекрытия в сечении
- плитка: сетка швов по формату, ▲ — ось старта
- О1 — марка отделки по реестру отделки альбома
- А — марка развёртки: буква стены, стрелка — взгляд

Ведомость отделки (на листе)

Марка	Поверхность	Материал, изделие	Цвет, код	Кол.
О4	потолок	окраска, Tikkurila Euro Power 7, матовая, подготовка Q3	Tikkurila G503 «Calla»	1,9 м²
О6	стены	облицовка плиткой, 600×1200×9 мм, аналог: керамогранит под травертин, матовый, затирка CG2WA		4 м²

Допущения и предложения на листе

Основа листа: планировка по обводу плана заказчика, не замерена (К-1); высота до плиты 2650 мм от чистого пола — решение автора (ИЗ-1); отметки плана потолков сдвинуты на -95 мм (+2.745 плана = низ плиты), не замерено (К-2); толщины стен приняты: наружные 260 мм, перегородки 130 мм (К-1); положение стен и проёмов — по брифу без обмера и плана БТИ (К-1); разрешённая мощность 10 кВт принята, ТУ не переданы (К-6); вентканалы приняты, в брифе не заданы (К-5); тип дома, перекрытие и несущие стены не известны — документов нет (К-3); плита электрическая — принята, в брифе не указано (К-6); система заземления TN-C-S принята, ТУ не переданы (К-6); число жильцов 2 принято, в брифе не указано (К-9); подрайон климата не задан — принят не северный (жилые от 2,5 м) (К-26).

Знак «**» — предложение проектировщика, заказчиком не утверждено (согласовать с заказчиком): К-1: дверь пом. 2 (стена В) — проём принят по обводу плана заказчика, без обмера: положение и ширина сняты с плана, не замерены; открывание наружу (в прихожую): санузел 1,1 м — внутрь полотно задевает раковину П14.

См. лист открытых вопросов (лист 5, записи К-1, К-3, К-5, К-6, К-9; лист 6, запись К-26).

Примечания

1. Развёртки — вид на стену изнутри помещения, по часовой стрелке; расположение — на схеме листа и на листе 71; размеры — в мм по чистовым поверхностям; отметки — в м от ±0,000; высоты Н — от чистого пола помещения до оси изделия, у декора — до центра.
2. Стена Г показана двумя видами: здесь — архитектурная развёртка (мебель, отделка, проёмы, высоты), электроточки и выводы ВК с привязками и таблицей — на листе 78 («Привязки»).
3. Схема мебели, приборов и декора не является технической документацией для производства мебели; габариты — по паспортам изделий.
4. Облицовка — по сетке швов 2 мм, раскладка от оси стены (треугольник у пола), целые ряды от пола; подрезки — по листу раскладки плитки.
5. Гидроизоляция в 2 слоя, заход на стены 200 мм — до облицовки, с актом скрытых работ и тестом проливом (узел — на листе узлов).
6. Картины и зеркала крепить к основанию по паспорту изделия (закладные и анкеры — в перечне скрытых работ); крест — ось центра предмета.

1000 мм · печать 1:1

Изм.	Кол.уч	Лист	№ док.	Подп.	Дата
Разраб.		Кырлан А.С.			04.11.26
Пров.					
ГИП					
Н. контр.					
Утв.					

ГД-2026-020-АИ

Квартира 68 м², элитный модерн

Общая площадь 68,47* м² · * размеры приняты, не замерены (реестр — л. 5–7, К-1)

Дизайн-проект интерьера

Стадия	Лист	Листов
РП	77	105

Развёртка стены Г. Санузел (пом. 2)

М 1:20

Кырлан Александр Сергеевич

выпуск 04.11.2026 № 8be4ef4c81 · стр. 86 из 117

Привязки электроточек и выводов ВК, стена Г. Санузел (пом. 2)

Санузел (пом. 2) · вид изнутри помещения · привязки в мм, отметки в м · к развёртке на листе 77

ПРЕДВАРИТЕЛЬНО · не для производства работ · открыто пунктов: 25 (реестр — л. 5–7)

Развёртка стены Г: электроточки и выводы

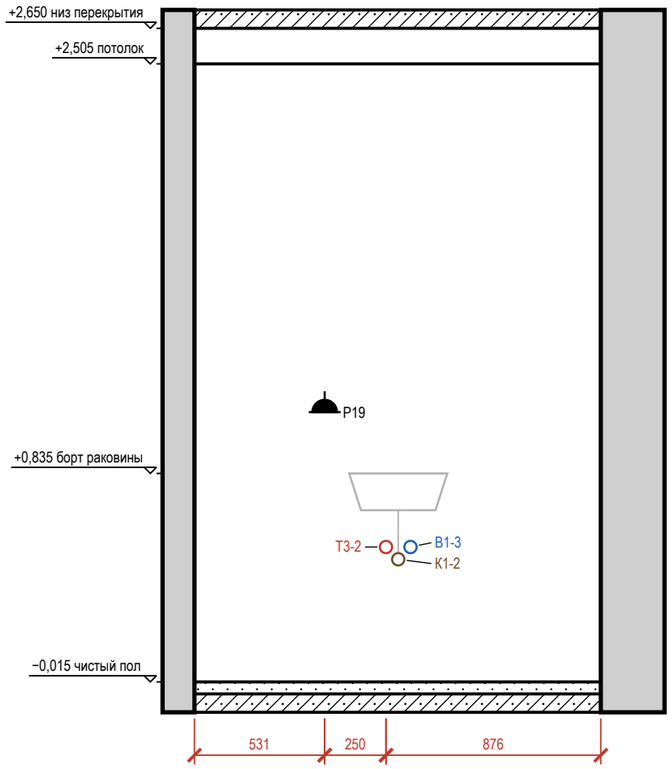



Таблица привязок электроточек и выводов

Марка	Назначение	От угла, мм	Н от пола, мм	Примечание
P19	розетка: розетка у раковины (фен, зона 3)	531	1100	гр. 15, IP44
T3-2	горячая вода — умывальник	781	550	межос. 100
K1-2	канализация — умывальник	831	500	Ø40
B1-3	холодная вода — умывальник	881	550	межос. 100

Условные обозначения

- розетка влагозащищённая IP44
- вывод B1 (код — в ведомости привязок)
- вывод T3 (код — в ведомости привязок)
- вывод K1 (код — в ведомости привязок)
- привязки точек и выводов от угла и от пола, мм
- A — марка развёртки: буква стены, стрелка — взгляд

Схема развёрток (М 1:50)

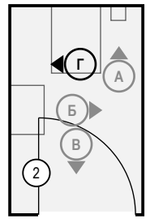

Примечания

1. Вид «Привязки» стены Г — электроточки и выводы ВК; архитектурная развёртка (мебель, отделка, проёмы, высоты) — на листе 77, расположение — на листе 71. Мебель и приборы — подложкой для ориентира; их марки и обозначения мебели, проёмов и стен — там же.
2. Привязки — в мм: по горизонтали от левого чистового угла стены до оси изделия, Н — от чистого пола до оси; все точки — в таблице привязок. Красная цепочка — привязки по осям; точки ближе 150 мм одна к другой в цепочку не дробятся — их привязки только в таблице.
3. У знака — марка электроточки (Р — розетка, S — выключатель, Св — светильник, ЭВ — вывод кабеля); посты в рамке и группа щита — в графе «Примечание»; группы по клавишам выключателя — на листе выключателей.
4. Коды выводов ВК: В1 — холодная вода, Т3 — горячая вода, К1 — канализация; номер после дефиса — номер вывода на листе выводов сантехники.

Допущения и предложения на листе

Основа листа: планировка по обводу плана заказчика, не замерена (К-1); высота до плиты 2650 мм от чистого пола — решение автора (ИЗ-1); отметки плана потолков сдвинуты на -95 мм (+2.745 плана = низ плиты), не замерено (К-2); толщины стен приняты: наружные 260 мм, перегородки 130 мм (К-1); положение стен и проёмов — по брифу без обмера и плана БТИ (К-1); разрешённая мощность 10 кВт принята, ТУ не переданы (К-6); вентканалы приняты, в брифе не заданы (К-5); тип дома, перекрытие и несущие стены не известны — документов нет (К-3); плита электрическая — принята, в брифе не указано (К-6); система заземления TN-C-S принята, ТУ не переданы (К-6); число жильцов 2 принято, в брифе не указано (К-9); подрайон климата не задан — принят не северный (жилые от 2,5 м) (К-26).

Знак «**» — предложение проектировщика, заказчиком не утверждено (согласовать с заказчиком): К-1: дверь пом. 2 (стена В) — проём принят по обводу плана заказчика, без обмера: положение и ширина сняты с плана, не замерены; открывание наружу (в прихожую): санузел 1,1 м — внутрь полотно задевает раковину П14.

См. лист открытых вопросов (лист 5, записи К-1, К-3, К-5, К-6, К-9; лист 6, запись К-26).

1000 мм · печать 1:1

Изм.	Кол.уч	Лист	№ док.	Подп.	Дата
Разраб.		Кырлан А.С.			04.11.26
Пров.					
ГИП					
Н. контр.					
Утв.					

ГД-2026-020-АИ

Квартира 68 м², элитный модерн

Общая площадь 68,47* м² · * размеры приняты, не замерены (реестр — л. 5–7, К-1)

Дизайн-проект интерьера

Стадия	Лист	Листов
РП	78	105

Привязки электроточек и выводов ВК, стена Г. Санузел (пом. 2)

М 1:25

Кырлан Александр Сергеевич


выпуск 04.11.2026 № 8be4ef4c81 · стр. 87 из 117

Развёртки стен А, Б. Ванная (пом. 3)

Ванная (пом. 3) · вид изнутри помещения · размеры в мм, отметки в м


ПРЕДВАРИТЕЛЬНО · не для производства работ · открыто пунктов: 25 (реестр — л. 5–7)

Развёртка стены А

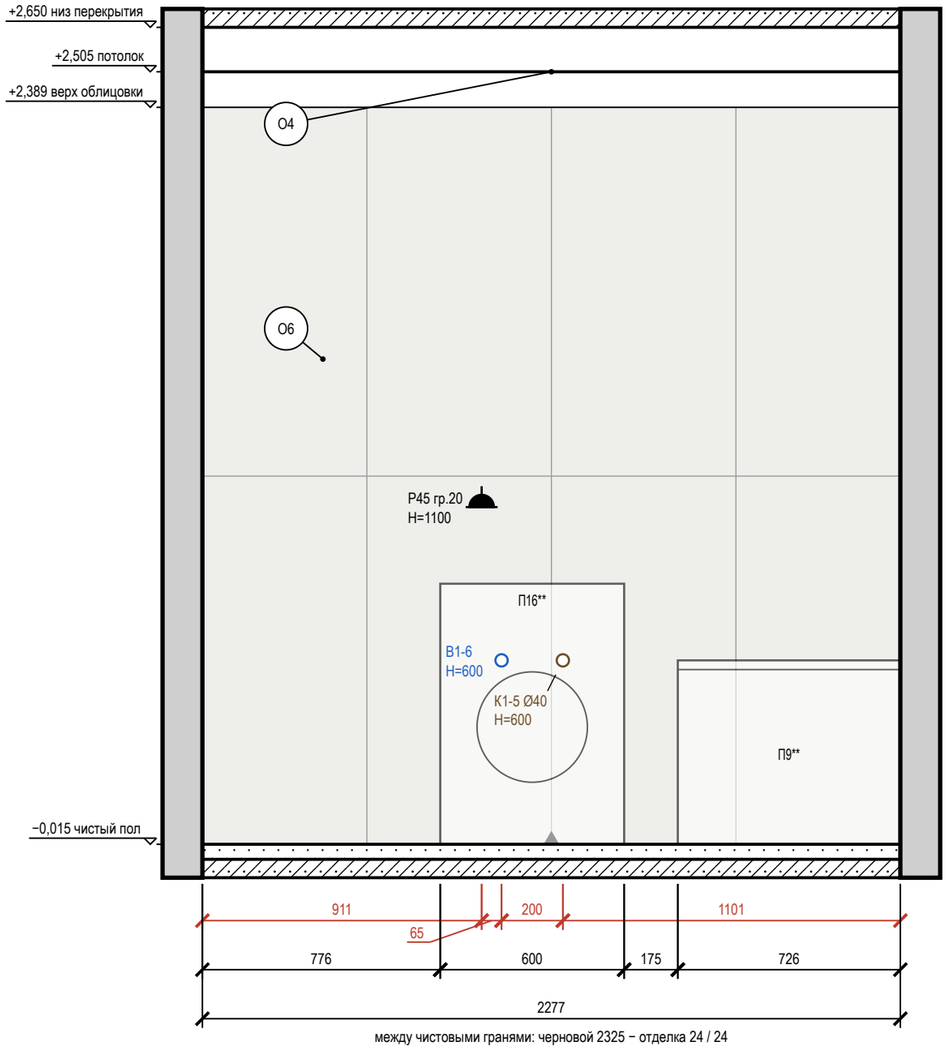


между чистовыми гранями: черновой 2325 − отделка 24 / 24

Развёртка стены Б

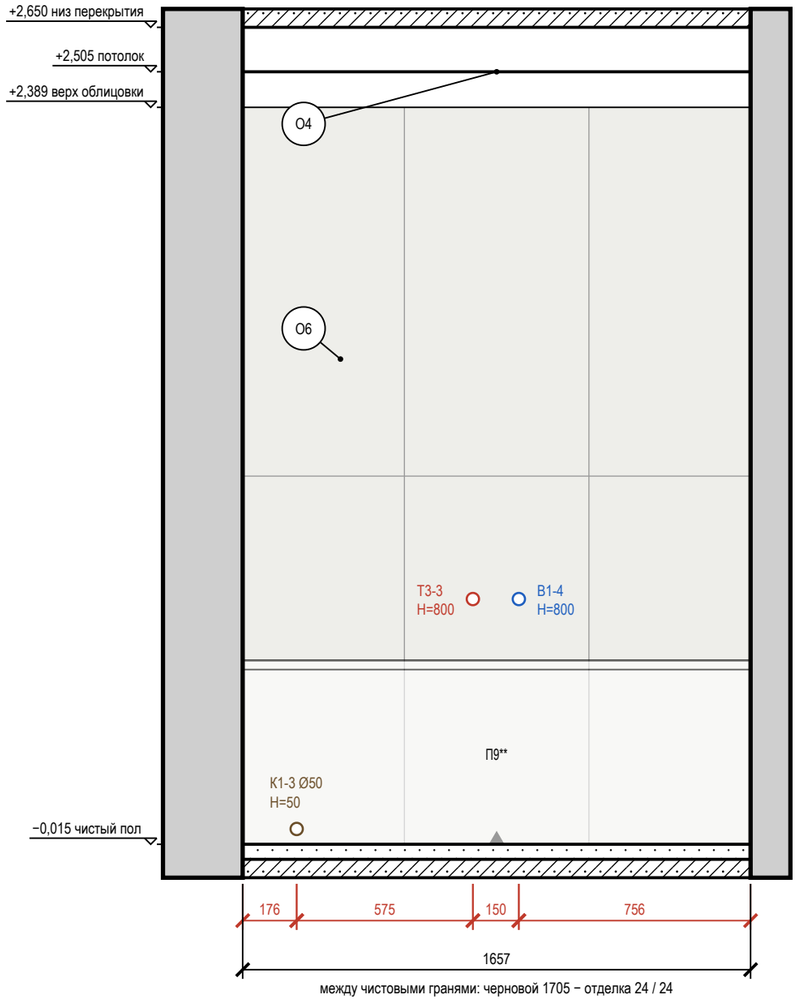

между чистовыми гранями: черновой 1705 − отделка 24 / 24

Схема развёрток (М 1:100)

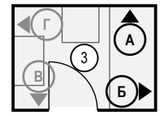

Условные обозначения

- розетка влагозащищённая IP44
- вывод В1 (код — в ведомости привязок)
- вывод Т3 (код — в ведомости привязок)
- вывод К1 (код — в ведомости привязок)
- привязки точек и выводов от угла и от пола, мм
- мебель и приборы — фасад по расстановке (условно)
- стены и перекрытия в сечении
- плитка: сетка швов по формату, ▲ — ось старта
- О1 — марка отделки по реестру отделки альбома
- А — марка развёртки: буква стены, стрелка — взгляд

Допущения и предложения на листе

Основа листа: планировка по обводу плана заказчика, не замерена (К-1); высота до плиты 2650 мм от чистого пола — решение автора (ИЗ-1); отметки плана потолков сдвинуты на -95 мм (+2.745 плана = низ плиты), не замерено (К-2); толщины стен приняты: наружные 260 мм, перегородки 130 мм (К-1); положение стен и проёмов — по брифу без обмера и плана БТИ (К-1); разрешённая мощность 10 кВт принята, ТУ не переданы (К-6); вентканалы приняты, в брифе не заданы (К-5); тип дома, перекрытие и несущие стены не известны — документов нет (К-3); плита электрическая — принята, в брифе не указано (К-6); система заземления TN-C-S принята, ТУ не переданы (К-6); число жильцов 2 принято, в брифе не указано (К-9); подрайон климата не задан — принят не северный (жилые от 2,5 м) (К-26).

Знак «*» — принято, не замерено и не подтверждено (замерить на объекте): К-1: дверь пом. 3 (стена В) — проём принят по обводу плана заказчика, без обмера: положение и ширина сняты с плана, не замерены.

Знак «**» — предложение проектировщика, заказчиком не утверждено (согласовать с заказчиком): ИЗ-3, К-7: П16 — место стиральной машины — в ванной у верхней стены, правее короба стояка; подход 1100 мм перед дверцей, выводы ХВС и К1 Ø40 за машиной; ИЗ-3, К-28: П9 — ванна 1700 × 750 у правой стены на всю глубину помещения (1700 мм по плану) — стояк в левом углу свободен. См. лист открытых вопросов (лист 5, записи К-1, К-3, К-5–К-7, К-9; лист 6, запись К-26; лист 7, записи ИЗ-3, К-28).

Примечания

1. Развёртки — вид на стену изнутри помещения, по часовой стрелке; расположение — на схеме листа и на листе 71; размеры — в мм по чистовым поверхностям; отметки — в м от ±0,000; высоты Н — от чистого пола помещения до оси изделия, у декора — до центра.
2. Красная цепочка — привязки электроточек и выводов по осям от угла чистовых стен; высота Н — у знака, от чистого пола до оси; высоты мебели, проёмов и границ отделки — колонкой отметок слева. Стена с 5 и более точками или с мелкими звеньями привязок показана двумя видами: архитектурная развёртка (мебель, отделка, проёмы, высоты) и вид «Привязки» на отдельном листе — точки и выводы с марками, одна цепочка по осям и таблица привязок (каждая точка — строка).
3. У знака электроточки: марка (Р — розетка, S — выключатель, Св — светильник, ЭВ — вывод кабеля), ×N — число постов в рамке, гр. — группа щита, Н — высота оси от чистого пола, мм; группы по клавишам выключателя — на листе выключателей.
4. Схема мебели, приборов и декора не является технической документацией для производства мебели; габариты — по паспортам изделий.
5. Облицовка — по сетке швов 2 мм, раскладка от оси стены (треугольник у пола), целые ряды от пола; подрезки — по листу раскладки плитки.
6. Гидроизоляция в 2 слоя, заход на стены 200 мм; над ванной — до 2000 и 300 мм за борт — до облицовки, с актом скрытых работ и тестом проливом (узел — на листе узлов).

1000 мм · печать 1:1

Изм.	Кол.уч	Лист	№ док.	Подп.	Дата
Разраб.		Кырлан А.С.			04.11.26
Пров.					
ГИП					
Н. контр.					
Утв.					

ГД-2026-020-АИ

Квартира 68 м², элитный модерн

Общая площадь 68,47* м² · * размеры приняты, не замерены (реестр — л. 5–7, К-1)

Дизайн-проект интерьера

Стадия	Лист	Листов
РП	79	105

Развёртки стен А, Б. Ванная (пом. 3)

М 1:20

Кырлан Александр Сергеевич


выпуск 04.11.2026 № 8be4ef4c81 · стр. 88 из 117

Развёртки стен В, Г. Ванная (пом. 3)

Ванная (пом. 3) · вид изнутри помещения · размеры в мм, отметки в м


ПРЕДВАРИТЕЛЬНО · не для производства работ · открыто пунктов: 25 (реестр — л. 5–7)

Развёртка стены В

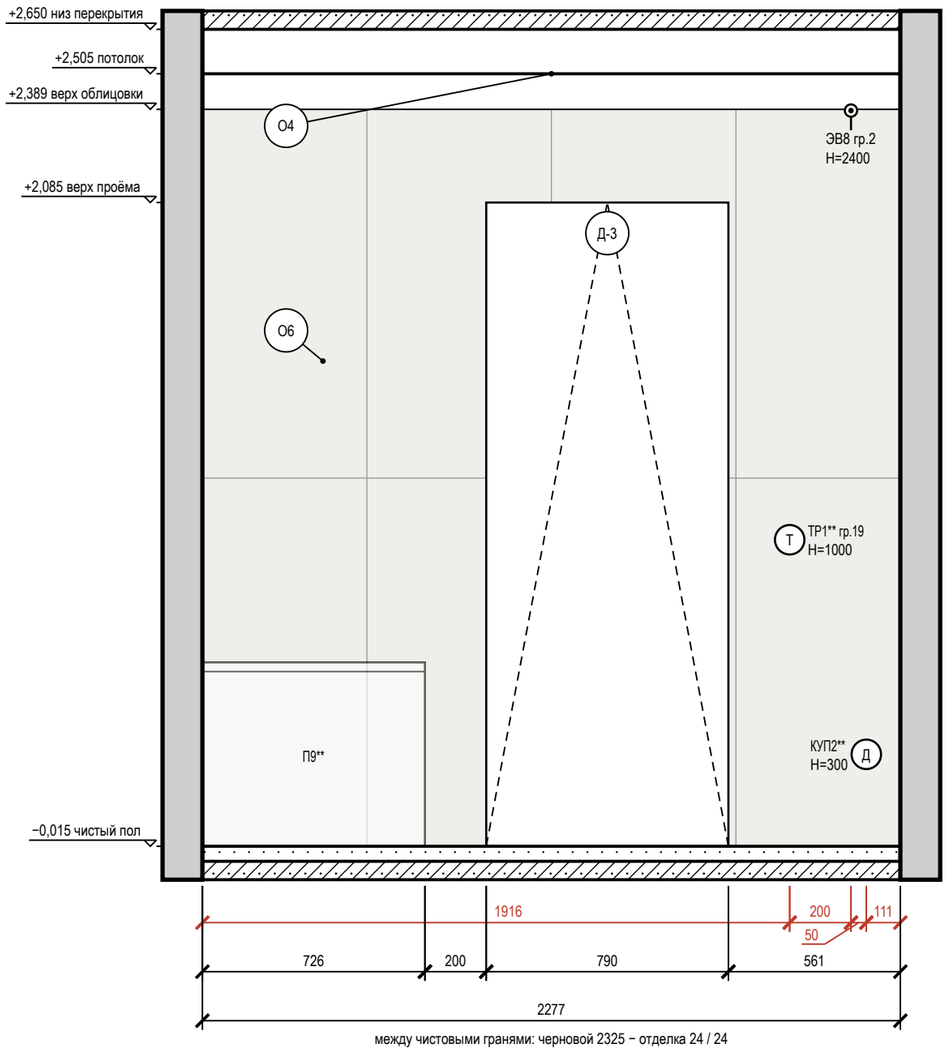


между чистовыми гранями: черновой 2325 − отделка 24 / 24

Развёртка стены Г

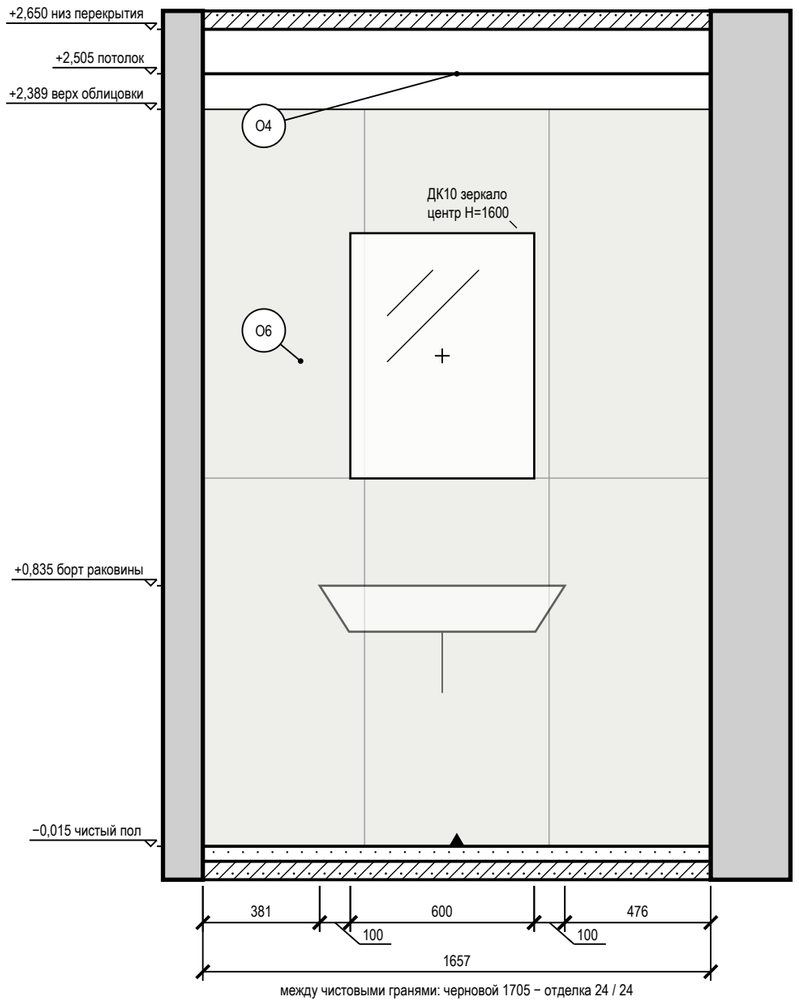

между чистовыми гранями: черновой 1705 − отделка 24 / 24

Схема развёрток (М 1:100)

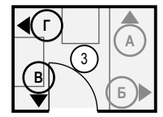

Условные обозначения

- вывод кабеля для подключения прибора (без розетки), марка ЭВ
- Т — терморегулятор тёплого пола
- привязки точек и выводов от угла и от пола, мм
- мебель и приборы — фасад по расстановке (условно)
- зеркало: марка Д, крест — центр, Н — высота центра, мм
- дверной проём; марка двери — в кружке
- стены и перекрытия в сечении
- плитка: сетка швов по формату, ▲ — ось старта
- О1 — марка отделки по реестру отделки альбома
- А — марка развёртки: буква стены, стрелка — взгляд

Допущения и предложения на листе

Основа листа: планировка по обводу плана заказчика, не замерена (К-1); высота до плиты 2650 мм от чистого пола — решение автора (ИЗ-1); отметки плана потолков сдвинуты на -95 мм (+2.745 плана = низ плиты), не замерено (К-2); толщины стен приняты: наружные 260 мм, перегородки 130 мм (К-1); положение стен и проёмов — по брифу без обмера и плана БТИ (К-1); разрешённая мощность 10 кВт принята, ТУ не переданы (К-6); вентканалы приняты, в брифе не заданы (К-5); тип дома, перекрытие и несущие стены не известны — документов нет (К-3); плита электрическая — принята, в брифе не указано (К-6); система заземления TN-C-S принята, ТУ не переданы (К-6); число жильцов 2 принято, в брифе не указано (К-9); подрайон климата не задан — принят не северный (жилые от 2,5 м) (К-26).

Знак «*» — принято, не замерено и не подтверждено (замерить на объекте): К-1: дверь пом. 3 (стена В) — проём принят по обводу плана заказчика, без обмера: положение и ширина сняты с плана, не замерены.

Знак «**» — предложение проектировщика, заказчиком не утверждено (согласовать с заказчиком): ТР1 — электрический тёплый пол в санузле — предложение по умолчанию (комфорт): мат 160 Вт (150 Вт/м² — типовой нагревательный мат, марка не выбрана) под свободным от мебели и приборов участком 1.3×0.8 м, датчик в гофре; плиточник и сантехник увязывают раскладку и стяжку; КУП2 — коробка уравнивания потенциалов, проводник от шины PE; ИЗ-3, К-28: П9 — ванна 1700 × 750 у правой стены на всю глубину помещения (1700 мм по плану) — стояк в левом углу свободен.

См. лист открытых вопросов (лист 5, записи К-1, К-3, К-5, К-6, К-9; лист 6, запись К-26; лист 7, записи ИЗ-3, К-28).

Примечания

1. Развёртки — вид на стену изнутри помещения, по часовой стрелке; расположение — на схеме листа и на листе 71; размеры — в мм по чистовым поверхностям; отметки — в м от ±0,000; высоты Н — от чистого пола помещения до оси изделия, у декора — до центра.
2. Красная цепочка — привязки электроточек и выводов по осям от угла чистовых стен; высота Н — у знака, от чистого пола до оси; высоты мебели, проёмов и границ отделки — колонкой отметок слева. Стена с 5 и более точками или с мелкими звеньями привязок показана двумя видами: архитектурная развёртка (мебель, отделка, проёмы, высоты) и вид «Привязки» на отдельном листе — точки и выводы с марками, одна цепочка по осям и таблица привязок (каждая точка — строка).
3. Стена Г показана двумя видами: здесь — архитектурная развёртка (мебель, отделка, проёмы, высоты), электроточки и выводы ВК с привязками и таблицей — на листе 81 («Привязки»).
4. У знака электроточки: марка (Р — розетка, S — выключатель, Св — светильник, ЭВ — вывод кабеля), ×N — число постов в рамке, гр. — группа щита, Н — высота оси от чистого пола, мм; группы по клавишам выключателя — на листе выключателей.
5. Схема мебели, приборов и декора не является технической документацией для производства мебели; габариты — по паспортам изделий.
6. Облицовка — по сетке швов 2 мм, раскладка от оси стены (треугольник у пола), целые ряды от пола; подрезки — по листу раскладки плитки.
7. Гидроизоляция в 2 слоя, заход на стены 200 мм; над ванной — до 2000 и 300 мм за борт — до облицовки, с актом скрытых работ и тестом проливом (узел — на листе узлов).
8. Картины и зеркала крепить к основанию по паспорту изделия (закладные и анкеры — в перечне скрытых работ); крест — ось центра предмета.

1000 мм · печать 1:1

Изм.	Кол.уч	Лист	№ док.	Подп.	Дата
Разраб.		Кырлан А.С.			04.11.26
Пров.					
ГИП					
Н. контр.					
Утв.					

ГД-2026-020-АИ

Квартира 68 м², элитный модерн

Общая площадь 68,47* м² · * размеры приняты, не замерены (реестр — л. 5–7, К-1)

Дизайн-проект интерьера	Стадия	Лист	Листов
	РП	80	105

Развёртки стен В, Г. Ванная (пом. 3)

М 1:20

Кырлан Александр Сергеевич

выпуск 04.11.2026 № 8be4ef4c81 · стр. 89 из 117

Привязки электроточек и выводов ВК, стена Г. Ванная (пом. 3)

Ванная (пом. 3) · вид изнутри помещения · привязки в мм, отметки в м · к развёртке на листе 80

ПРЕДВАРИТЕЛЬНО · не для производства работ · открыто пунктов: 25 (реестр — л. 5–7)

Развёртка стены Г: электроточки и выводы

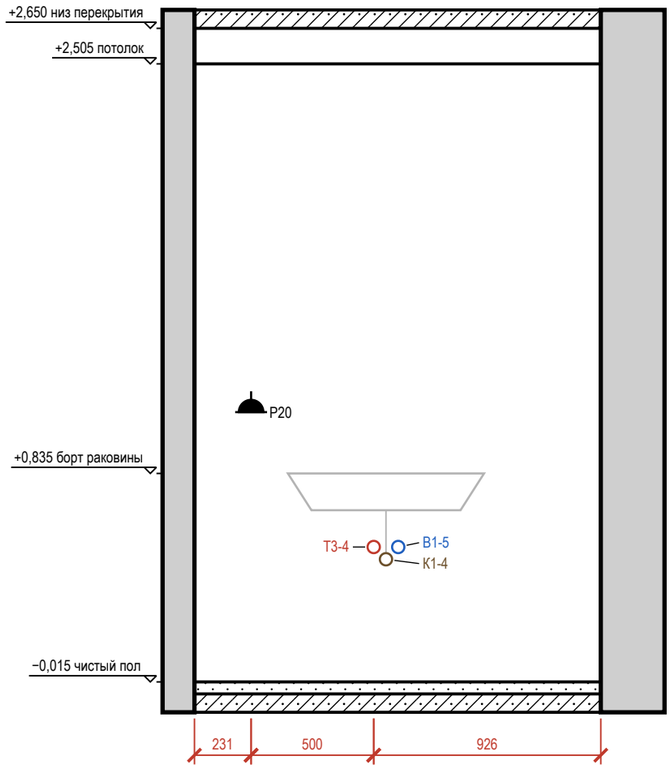



Таблица привязок электроточек и выводов

Марка	Назначение	От угла, мм	Н от пола, мм	Примечание
P20	розетка: фен у умывальника	231	1100	гр. 15, IP44
T3-4	горячая вода — умывальник	731	550	межос. 100
K1-4	канализация — умывальник	781	500	Ø40
B1-5	холодная вода — умывальник	831	550	межос. 100

Условные обозначения

- розетка влагозащищённая IP44
- вывод B1 (код — в ведомости привязок)
- вывод T3 (код — в ведомости привязок)
- вывод K1 (код — в ведомости привязок)
- привязки точек и выводов от угла и от пола, мм
- марка развёртки: буква стены, стрелка — взгляд

Схема развёрток (М 1:50)

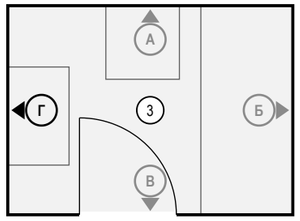

Примечания

1. Вид «Привязки» стены Г — электроточки и выводы ВК; архитектурная развёртка (мебель, отделка, проёмы, высоты) — на листе 80, расположение — на листе 71. Мебель и приборы — подложкой для ориентира; их марки и обозначения мебели, проёмов и стен — там же.
2. Привязки — в мм: по горизонтали от левого чистового угла стены до оси изделия, Н — от чистого пола до оси; все точки — в таблице привязок. Красная цепочка — привязки по осям; точки ближе 150 мм одна к другой в цепочку не дробятся — их привязки только в таблице.
3. У знака — марка электроточки (Р — розетка, S — выключатель, Св — светильник, ЭВ — вывод кабеля); посты в рамке и группа щита — в графе «Примечание»; группы по клавишам выключателя — на листе выключателей.
4. Коды выводов ВК: В1 — холодная вода, Т3 — горячая вода, К1 — канализация; номер после дефиса — номер вывода на листе выводов сантехники.

Допущения и предложения на листе

Основа листа: планировка по обводу плана заказчика, не замерена (К-1); высота до плиты 2650 мм от чистого пола — решение автора (ИЗ-1); отметки плана потолков сдвинуты на -95 мм (+2.745 плана = низ плиты), не замерено (К-2); толщины стен приняты: наружные 260 мм, перегородки 130 мм (К-1); положение стен и проёмов — по брифу без обмера и плана БТИ (К-1); разрешённая мощность 10 кВт принята, ТУ не переданы (К-6); вентканалы приняты, в брифе не заданы (К-5); тип дома, перекрытие и несущие стены не известны — документов нет (К-3); плита электрическая — принята, в брифе не указано (К-6); система заземления TN-C-S принята, ТУ не переданы (К-6); число жильцов 2 принято, в брифе не указано (К-9); подрайон климата не задан — принят не северный (жилые от 2,5 м) (К-26).

Знак «*» — принято, не замерено и не подтверждено (замерить на объекте): К-1: дверь пом. 3 (стена В) — проём принят по обводу плана заказчика, без обмера: положение и ширина сняты с плана, не замерены.

См. лист открытых вопросов (лист 5, записи К-1, К-3, К-5, К-6, К-9; лист 6, запись К-26).

1000 мм · печать 1:1

Изм.	Кол.уч	Лист	№ док.	Подп.	Дата
Разраб.		Кырлан А.С.			04.11.26
Пров.					
ГИП					
Н. контр.					
Утв.					

ГД-2026-020-АИ

Квартира 68 м², элитный модерн

Общая площадь 68,47* м² · * размеры приняты, не замерены (реестр — л. 5–7, К-1)

Дизайн-проект интерьера

Стадия	Лист	Листов
РП	81	105

Привязки электроточек и выводов ВК, стена Г. Ванная (пом. 3)

М 1:25

Кырлан Александр Сергеевич


выпуск 04.11.2026 № 8be4ef4c81 · стр. 90 из 117

Развёртка стены А. Прихожая (пом. 4)

Прихожая (пом. 4) · вид изнутри помещения · размеры в мм, отметки в м


ПРЕДВАРИТЕЛЬНО · не для производства работ · открыто пунктов: 25 (реестр — л. 5–7)

Развёртка стены А

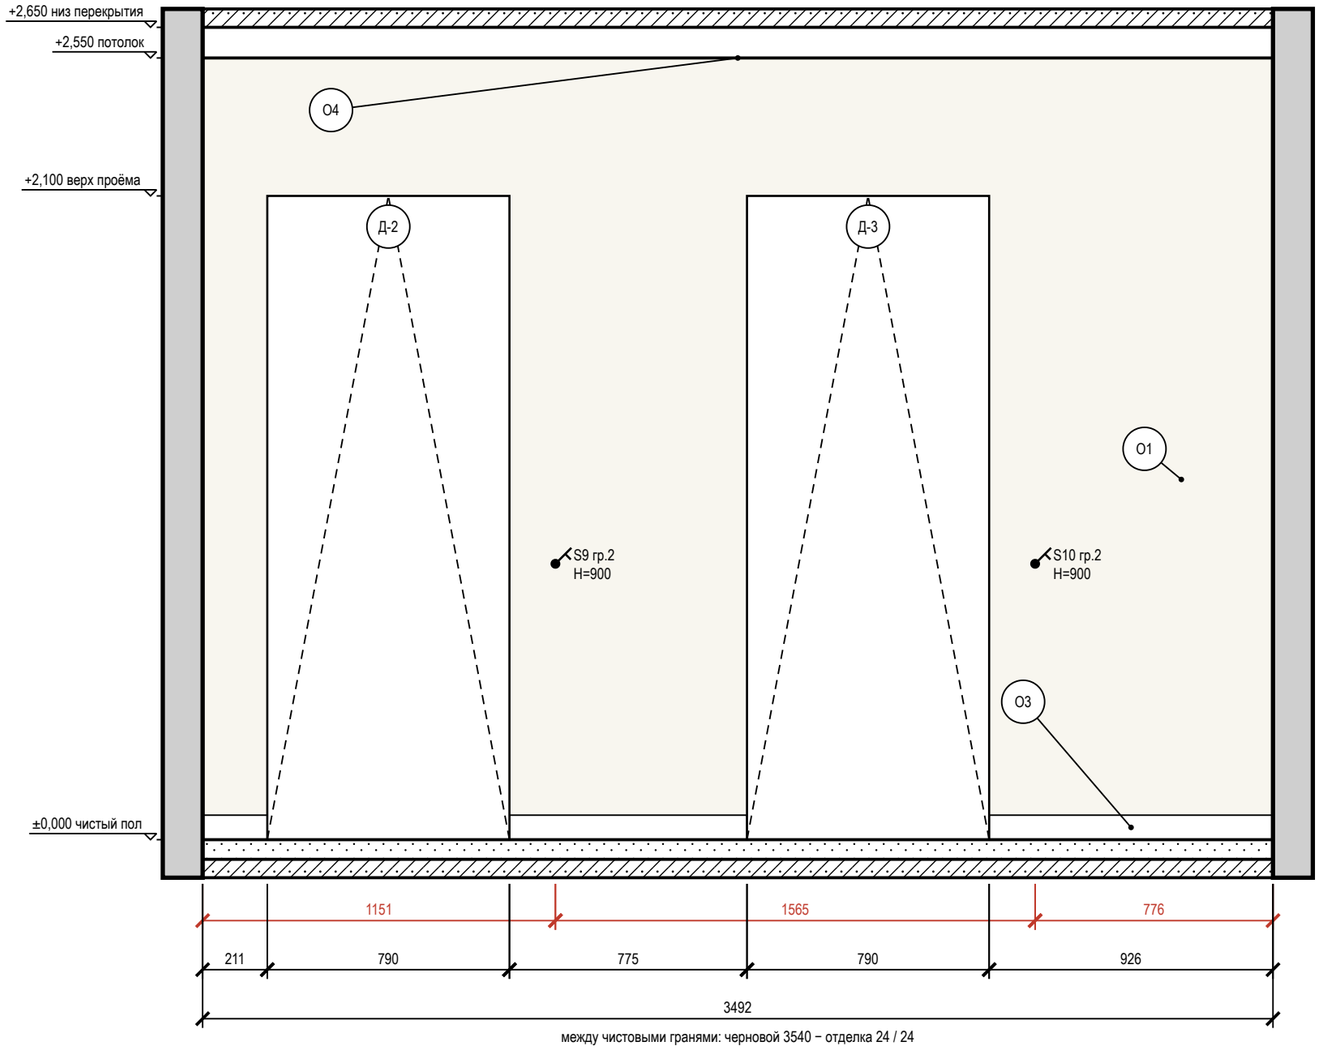

между чистовыми гранями: черновой 3540 − отделка 24 / 24

Схема развёрток (М 1:100)

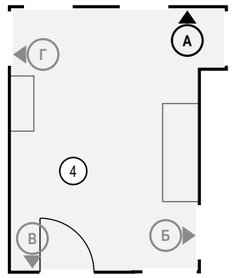

Условные обозначения

- выключатель одноклавишный
- привязки точек и выводов от угла и от пола, мм
- мебель и приборы — фасад по расстановке (условно)
- дверной проём; марка двери — в кружке
- стены и перекрытия в сечении
- окраска: тон — цвет по коду производителя (условно)
- О1 — марка отделки по реестру отделки альбома
- А — марка развёртки: буква стены, стрелка — взгляд

Ведомость отделки (на листе)

Марка	Поверхность	Материал, изделие	Цвет, код	Кол.
О1	стены	окраска, Farrow & Ball Modern Emulsion, матовая, подготовка Q3	Farrow & Ball No. 2003 «Pointing»	5,6 м²
О3	плинтус	плинтус МДФ, h 80 мм, аналог: плинтус МДФ под покраску 80×16	Farrow & Ball No. 2003 «Pointing»	1,9 м
О4	потолок	окраска, Tikkurila Euro Power 7, глубокоматовая, подготовка Q3	Tikkurila G503 «Calla»	13,9 м²

Допущения и предложения на листе

Основа листа: планировка по обводу плана заказчика, не замерена (К-1); высота до плиты 2650 мм от чистого пола — решение автора (ИЗ-1); отметки плана потолков сдвинуты на -95 мм (+2.745 плана = низ плиты), не замерено (К-2); толщины стен приняты: наружные 260 мм, перегородки 130 мм (К-1); положение стен и проёмов — по брифу без обмера и плана БТИ (К-1); разрешённая мощность 10 кВт принята, ТУ не переданы (К-6); вентканалы приняты, в брифе не заданы (К-5); тип дома, перекрытие и несущие стены не известны — документов нет (К-3); плита электрическая — принята, в брифе не указано (К-6); система заземления TN-C-S принята, ТУ не переданы (К-6); число жильцов 2 принято, в брифе не указано (К-9); подрайон климата не задан — принят не северный (жилые от 2,5 м) (К-26).

Знак «*» — принято, не замерено и не подтверждено (замерить на объекте): К-1: дверь пом. 4 (стена В) — входная дверь: положение и ширина проёма приняты по обводу плана заказчика, без обмера, не замерены.

См. лист открытых вопросов (лист 5, записи К-1, К-3, К-5, К-6, К-9; лист 6, запись К-26).

Примечания

1. Развёртки — вид на стену изнутри помещения, по часовой стрелке; расположение — на схеме листа и на листе 71; размеры — в мм по чистовым поверхностям; отметки — в м от ±0,000; высоты Н — от чистого пола помещения до оси изделия, у декора — до центра.
2. Красная цепочка — привязки электроточек и выводов по осям от угла чистовых стен; высота Н — у знака, от чистого пола до оси; высоты мебели, проёмов и границ отделки — колонкой отметок слева. Стена с 5 и более точками или с мелкими звеньями привязок показана двумя видами: архитектурная развёртка (мебель, отделка, проёмы, высоты) и вид «Привязки» на отдельном листе — точки и выводы с марками, одна цепочка по осям и таблица привязок (каждая точка — строка).
3. У знака электроточки: марка (Р — розетка, S — выключатель, Св — светильник, ЭВ — вывод кабеля), ×N — число постов в рамке, гр. — группа щита, Н — высота оси от чистого пола, мм; группы по клавишам выключателя — на листе выключателей.
4. Схема мебели, приборов и декора не является технической документацией для производства мебели; габариты — по паспортам изделий.
5. Потолок — у каждой стены свой, по плану потолков (ПТ3); ступени — зоной, кромка короба перед нишей — тонкой линией; в поле потолка: ПТ4 +2,650.

1000 мм · печать 1:1

Изм.	Кол.уч	Лист	№ док.	Подп.	Дата
Разраб.		Кырлан А.С.			04.11.26
Пров.					
ГИП					
Н. контр.					
Утв.					

ГД-2026-020-АИ

Квартира 68 м², элитный модерн

Общая площадь 68,47* м² · * размеры приняты, не замерены (реестр — л. 5–7, К-1)

Дизайн-проект интерьера

Стадия	Лист	Листов
РП	82	105

Развёртка стены А. Прихожая (пом. 4)

М 1:20

Кырлан Александр Сергеевич


выпуск 04.11.2026 № 8be4ef4c81 · стр. 91 из 117

Развёртки стен Б, В. Прихожая (пом. 4)

Прихожая (пом. 4) · вид изнутри помещения · размеры в мм, отметки в м


ПРЕДВАРИТЕЛЬНО · не для производства работ · открыто пунктов: 25 (реестр — л. 5–7)

Развёртка стены Б

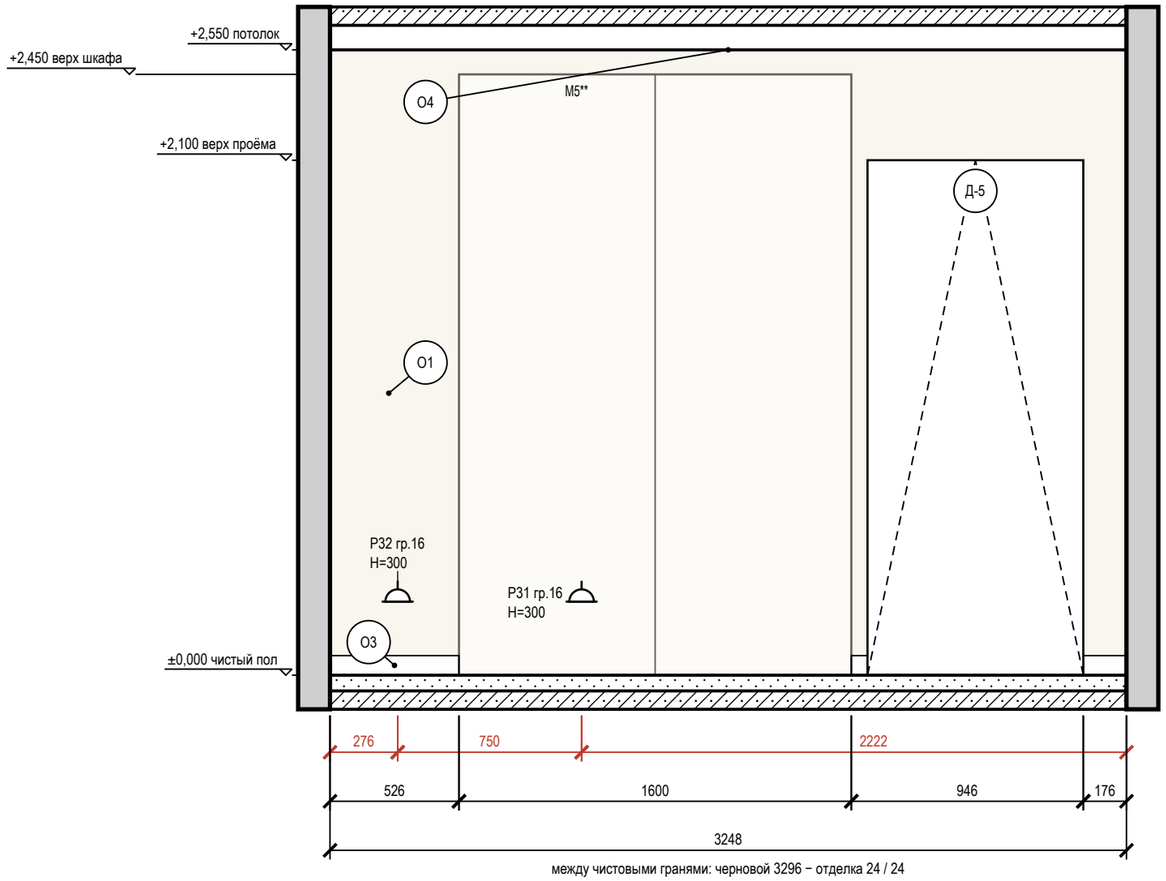


между чистовыми гранями: черновой 3296 − отделка 24 / 24

Развёртка стены В

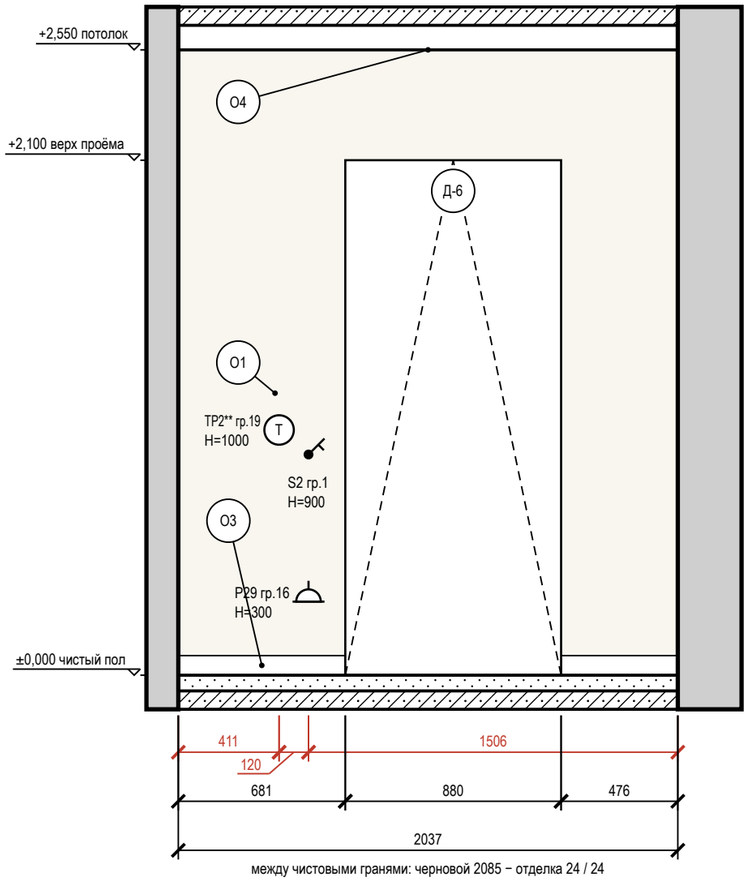

между чистовыми гранями: черновой 2085 − отделка 24 / 24

Схема развёрток (М 1:100)

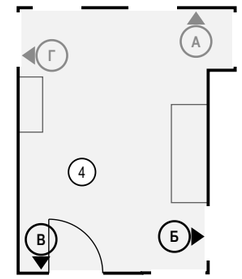

Допущения и предложения на листе. Основа листа: планировка по обводу плана заказчика, не замерена (К-1); высота до плиты 2650 мм от чистого пола — решение автора (ИЗ-1); отметки плана потолков сдвинуты на -95 мм (+2.745 плана = низ плиты), не замерено (К-2); толщины стен приняты: наружные 260 мм, перегородки 130 мм (К-1); положение стен и проёмов — по брифу без обмера и плана БТИ (К-1); разрешённая мощность 10 кВт принята, ТУ не переданы (К-6); вентканалы приняты, в брифе не заданы (К-5); тип дома, перекрытие и несущие стены не известны — документов нет (К-3); плита электрическая — принята, в брифе не указано (К-6); система заземления TN-C-S принята, ТУ не переданы (К-6); число жильцов 2 принято, в брифе не указано (К-9); подрайон климата не задан — принят не северный (жилые от 2,5 м) (К-26). Знак «*» — принято, не замерено и не подтверждено (замерить на объекте): К-1: дверь пом. 4 (стена В) — входная дверь: положение и ширина проёма приняты по обводу плана заказчика, без обмера, не замерены. Знак «**» — предложение проектировщика, заказчиком не утверждено (согласовать с заказчиком): ТР2 — электрический тёплый пол в прихожей — предложение по умолчанию (комфорт): мат 290 Вт (150 Вт/м² — типовой нагревательный мат, марка не выбрана) под свободным от мебели и приборов участком 1.1×1.9 м, датчик в гофре; плиточник и сантехник увязывают раскладку и стяжку. См. лист открытых вопросов (лист 5, записи К-1, К-3, К-5–К-7, К-9; лист 6, запись К-26).

Условные обозначения

- розетка с заземляющим контактом; у знака — марка, ×N постов в рамке, гр. — группа щита, Н — высота оси, мм
- выключатель одноклавишный
- (Т) терморегулятор тёплого пола
- привязки точек и выводов от угла и от пола, мм
- мебель и приборы — фасад по расстановке (условно)
- дверной проём; марка двери — в кружке
- стены и перекрытия в сечении
- окраска: тон — цвет по коду производителя (условно)
- (О1) марка отделки по реестру отделки альбома
- (А) марка развёртки: буква стены, стрелка — взгляд

Ведомость отделки (на листе)

Марка	Поверхность	Материал, изделие	Цвет, код	Кол.
О1	стены	окраска, Farrow & Ball Modern Emulsion, матовая, подготовка Q3	Farrow & Ball No. 2003 «Pointing»	9,8 м²
О3	плинтус	плинтус МДФ, h 80 мм, аналог: плинтус МДФ под покраску 80×16	Farrow & Ball No. 2003 «Pointing»	1,9 м
О4	потолок	окраска, Tikkurila Euro Power 7, глубокоматовая, подготовка Q3	Tikkurila G503 «Calla»	13,9 м²

Примечания

1. Развёртки — вид на стену изнутри помещения, по часовой стрелке; расположение — на схеме листа и на листе 71; размеры — в мм по чистовым поверхностям; отметки — в м от ±0,000; высоты Н — от чистого пола помещения до оси изделия, у декора — до центра.
2. Красная цепочка — привязки электроточек и выводов по осям от угла чистовых стен; высота Н — у знака, от чистого пола до оси; высоты мебели, проёмов и границ отделки — колонкой отметок слева. Стена с 5 и более точками или с мелкими звеньями привязок показана двумя видами: архитектурная развёртка (мебель, отделка, проёмы, высоты) и вид «Привязки» на отдельном листе — точки и выводы с марками, одна цепочка по осям и таблица привязок (каждая точка — строка).
3. У знака электроточки: марка (Р — розетка, S — выключатель, Св — светильник, ЭВ — вывод кабеля), ×N — число постов в рамке, гр. — группа щита, Н — высота оси от чистого пола, мм; группы по клавишам выключателя — на листе выключателей.
4. Схема мебели, приборов и декора не является технической документацией для производства мебели; габариты — по паспортам изделий.
5. Потолок — у каждой стены свой, по плану потолков (ПТ3); ступени — зоной, кромка короба перед нишей — тонкой линией; в поле потолка: ПТ4 +2,650.

1000 мм · печать 1:1

Изм.	Кол.уч	Лист	№ док.	Подп.	Дата
Разраб.		Кырлан А.С.			04.11.26
Пров.					
ГИП					
Н. контр.					
Утв.					

ГД-2026-020-АИ

Квартира 68 м², элитный модерн

Общая площадь 68,47* м² · * размеры приняты, не замерены (реестр — л. 5–7, К-1)

Дизайн-проект интерьера

Стадия	Лист	Листов
РП	83	105

Развёртки стен Б, В. Прихожая (пом. 4)

М 1:25

Кырлан Александр Сергеевич


выпуск 04.11.2026 № 8be4ef4c81 · стр. 92 из 117

Развёртка стены Г. Прихожая (пом. 4)

Прихожая (пом. 4) · вид изнутри помещения · размеры в мм, отметки в м

ПРЕДВАРИТЕЛЬНО · не для производства работ · открыто пунктов: 25 (реестр — л. 5–7)

Развёртка стены Г

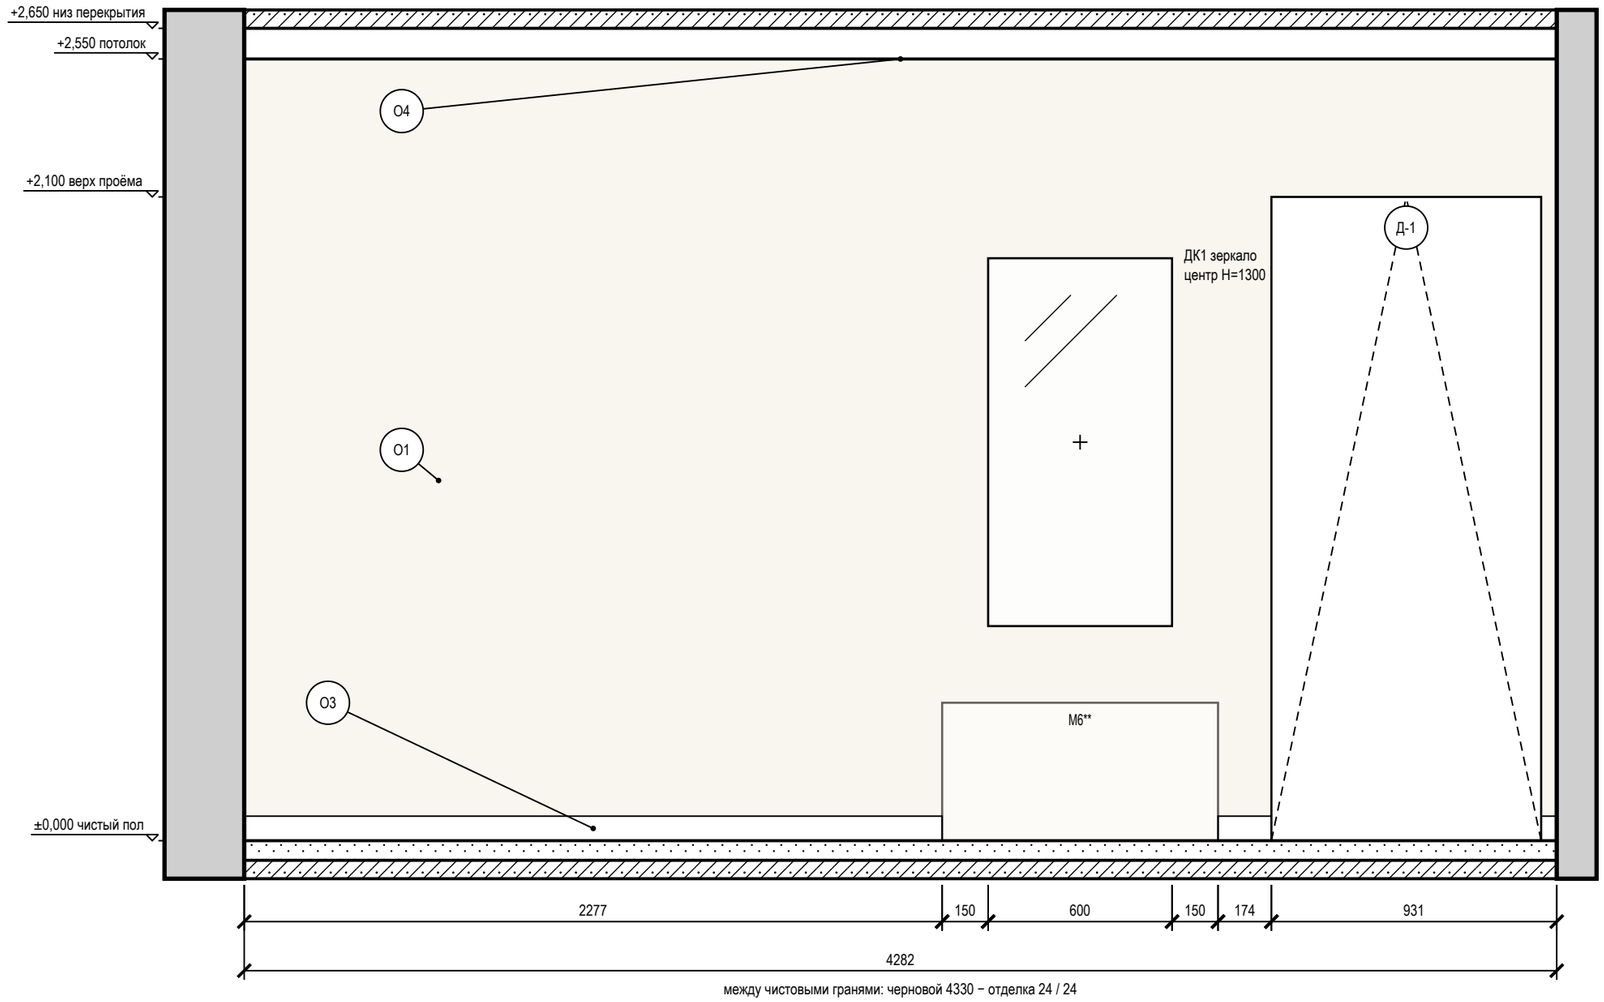

между чистовыми гранями: черновой 4330 − отделка 24 / 24

Допущения и предложения на листе

Основа листа: планировка по обводу плана заказчика, не замерена (К-1); высота до плиты 2650 мм от чистого пола — решение автора (ИЗ-1); отметки плана потолков сдвинуты на -95 мм (+2.745 плана = низ плиты), не замерено (К-2); толщины стен приняты: наружные 260 мм, перегородки 130 мм (К-1); положение стен и проёмов — по брифу без обмера и плана БТИ (К-1); разрешённая мощность 10 кВт принята, ТУ не переданы (К-6); вентканалы приняты, в брифе не заданы (К-5); тип дома, перекрытие и несущие стены не известны — документов нет (К-3); плита электрическая — принята, в брифе не указано (К-6); система заземления TN-C-S принята, ТУ не переданы (К-6); число жильцов 2 принято, в брифе не указано (К-9); подрайон климата не задан — принят не северный (жилые от 2,5 м) (К-26).

Знак «*» — принято, не замерено и не подтверждено (замерить на объекте): К-1: дверь пом. 4 (стена В) — входная дверь: положение и ширина проёма приняты по обводу плана заказчика, без обмера, не замерены.

Знак «**» — предложение проектировщика, заказчиком не утверждено (согласовать с заказчиком): М6 — сушилка для обуви под скамьёй — предложение по умолчанию (комфорт), заказчик может снять; питание — розетка «уборка, сушилка обуви».


См. лист открытых вопросов (лист 5, записи К-1, К-3, К-5, К-6, К-9; лист 6, запись К-26).

Примечания

1. Развёртки — вид на стену изнутри помещения, по часовой стрелке; расположение — на схеме листа и на листе 71; размеры — в мм по чистовым поверхностям; отметки — в м от ±0,000; высоты Н — от чистого пола помещения до оси изделия, у декора — до центра.
2. Стена Г показана двумя видами: здесь — архитектурная развёртка (мебель, отделка, проёмы, высоты), электроточки и выводы ВК с привязками и таблицей — на листе 85 («Привязки»).
3. Схема мебели, приборов и декора не является технической документацией для производства мебели; габариты — по паспортам изделий.
4. Картины и зеркала крепить к основанию по паспорту изделия (закладные и анкеры — в перечне скрытых работ); крест — ось центра предмета.
5. Потолок — у каждой стены свой, по плану потолков (ПТ3); ступени — зоной, кромка короба перед нишей — тонкой линией; в поле потолка: ПТ4 +2,650.

1000 мм · печать 1:1

Схема развёрток (М 1:100)

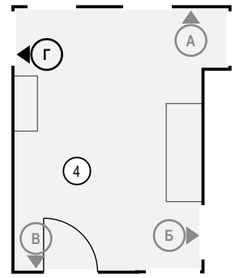

Условные обозначения

- мебель и приборы — фасад по расстановке (условно)
- зеркало: марка Д, крест — центр, Н — высота центра, мм
- дверной проём; марка двери — в кружке
- стены и перекрытия в сечении
- окраска: тон — цвет по коду производителя (условно)
- О1 — марка отделки по реестру отделки альбома
- А — марка развёртки: буква стены, стрелка — взгляд

Ведомость отделки (на листе)

Марка	Поверхность	Материал, изделие	Цвет, код	Кол.
О1	стены	окраска, Farrow & Ball Modern Emulsion, матовая, подготовка Q3	Farrow & Ball No. 2003 «Pointing»	9,1 м²
О3	плинтус	плинтус МДФ, h 80 мм, аналог: плинтус МДФ под покраску 80×16	Farrow & Ball No. 2003 «Pointing»	2,5 м
О4	потолок	окраска, Tikkurila Euro Power 7, глубокоматовая, подготовка Q3	Tikkurila G503 «Calla»	13,9 м²

Изм.	Кол.уч	Лист	№ док.	Подп.	Дата
Разраб.		Кырлан А.С.			04.11.26
Пров.					
ГИП					
Н. контр.					
Утв.					

ГД-2026-020-АИ

Квартира 68 м², элитный модерн

Общая площадь 68,47* м² · * размеры приняты, не замерены (реестр — л. 5–7, К-1)

Дизайн-проект интерьера

Стадия	Лист	Листов
РП	84	105

Развёртка стены Г. Прихожая (пом. 4)

М 1:20

Кырлан Александр Сергеевич

выпуск 04.11.2026 № 8be4ef4c81 · стр. 93 из 117

Привязки электроточек, стена Г. Прихожая (пом. 4)

Прихожая (пом. 4) · вид изнутри помещения · привязки в мм, отметки в м · к развёртке на листе 84

ПРЕДВАРИТЕЛЬНО · не для производства работ · открыто пунктов: 25 (реестр — л. 5–7)

Развёртка стены Г: электроточки и выводы

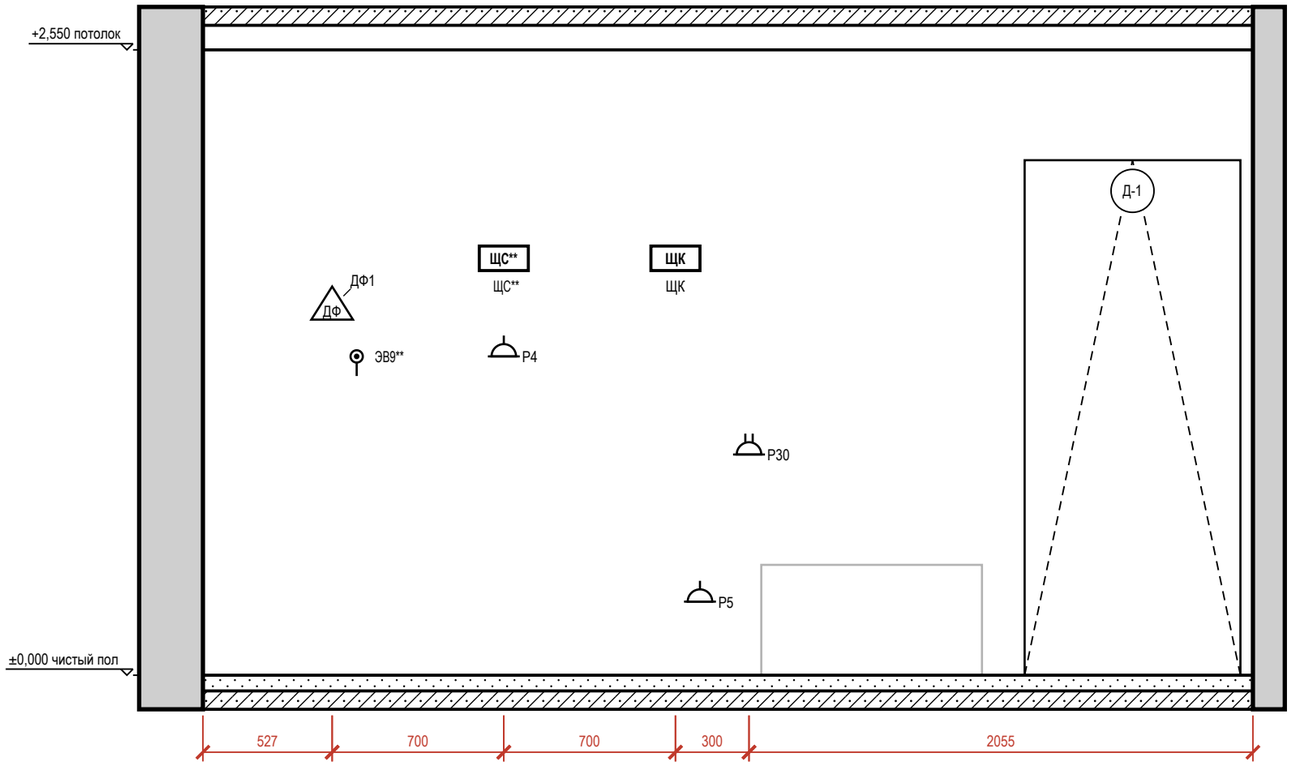



Таблица привязок электроточек и выводов

Марка	Назначение	От угла, мм	Н от пола, мм	Примечание
ДФ1	домофон: трубка домофона	527	1500	
ЭВ9**	вывод кабеля: контроллер защиты от протечек и питание электрокранов (у слаботочного щита)	627	1300	гр. 16
Р4	розетка: питание слаботочного щита (роутер, ONT)	1227	1300	гр. 16
ЩС**	щит: щит слаботочный: ввод провайдера, ONT, роутер	1227	1700	
ЩК	щит: щит квартирный ЩРВ-П-72, IP41	1927	1700	
Р5	розетка: уборка, сушилка обуви	2027	300	гр. 7
Р30	розетка: прихожая: зарядка телефона и ключей	2227	900	рамка 2 поста, гр. 16

Условные обозначения

- розетка с заземляющим контактом; у знака — марка, ×N постов в рамке, гр. — группа щита, Н — высота оси, мм
- вывод кабеля для подключения прибора (без розетки), марка ЭВ
- ДФ — трубка или монитор домофона
- ЩК — щит квартирный
- привязки точек и выводов от угла и от пола, мм
- А — марка развёртки: буква стены, стрелка — взгляд

Схема развёрток (М 1:100)

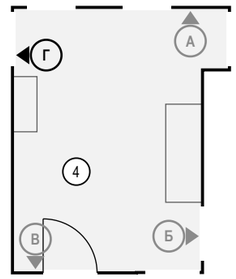

Примечания

1. Вид «Привязки» стены Г — электроточки и выводы ВК; архитектурная развёртка (мебель, отделка, проёмы, высоты) — на листе 84, расположение — на листе 71. Мебель и приборы — подложкой для ориентира; их марки и обозначения мебели, проёмов и стен — там же.
2. Привязки — в мм: по горизонтали от левого чистового угла стены до оси изделия, Н — от чистого пола до оси; все точки — в таблице привязок. Красная цепочка — привязки по осям; точки ближе 150 мм одна к другой в цепочку не дробятся — их привязки только в таблице.
3. У знака — марка электроточки (Р — розетка, S — выключатель, Св — светильник, ЭВ — вывод кабеля); посты в рамке и группа щита — в графе «Примечание»; группы по клавишам выключателя — на листе выключателей.

Допущения и предложения на листе

Основа листа: планировка по обводу плана заказчика, не замерена (К-1); высота до плиты 2650 мм от чистого пола — решение автора (ИЗ-1); отметки плана потолков сдвинуты на -95 мм (+2.745 плана = низ плиты), не замерено (К-2); толщины стен приняты: наружные 260 мм, перегородки 130 мм (К-1); положение стен и проёмов — по брифу без обмера и плана БТИ (К-1); разрешённая мощность 10 кВт принята, ТУ не переданы (К-6); вентканалы приняты, в брифе не заданы (К-5); тип дома, перекрытие и несущие стены не известны — документов нет (К-3); плита электрическая — принята, в брифе не указано (К-6); система заземления TN-C-S принята, ТУ не переданы (К-6); число жильцов 2 принято, в брифе не указано (К-9); подрайон климата не задан — принят не северный (жилые от 2,5 м) (К-26).

Знак «*» — принято, не замерено и не подтверждено (замерить на объекте): К-1: дверь пом. 4 (стена В) — входная дверь: положение и ширина проёма приняты по обводу плана заказчика, без обмера, не замерены.

Знак «**» — предложение проектировщика, заказчиком не утверждено (согласовать с заказчиком): ЭВ9 — питание контроллера защиты от протечек — предложение по умолчанию, вывод у ЩС в сухом помещении; ЩС — щит слаботочный: место и состав.

См. лист открытых вопросов (лист 5, записи К-1, К-3, К-5, К-6, К-9; лист 6, запись К-26).

1000 мм · печать 1:1

Изм.	Кол.уч	Лист	№ док.	Подп.	Дата
Разраб.		Кырлан А.С.			04.11.26
Пров.					
ГИП					
Н. контр.					
Утв.					

ГД-2026-020-АИ

Квартира 68 м², элитный модерн

Общая площадь 68,47* м² · * размеры приняты, не замерены (реестр — л. 5–7, К-1)

Дизайн-проект интерьера

Стадия	Лист	Листов
РП	85	105

Привязки электроточек, стена Г. Прихожая (пом. 4)

М 1:25

Кырлан Александр Сергеевич


выпуск 04.11.2026 № 8be4ef4c81 · стр. 94 из 117

Развёртка стены А1. Кухня-столовая (пом. 5), кухонный фронт

Кухня-столовая (пом. 5) · вид изнутри помещения · размеры в мм, отметки в м


ПРЕДВАРИТЕЛЬНО · не для производства работ · открыто пунктов: 25 (реестр — л. 5–7)

Развёртка стены А1

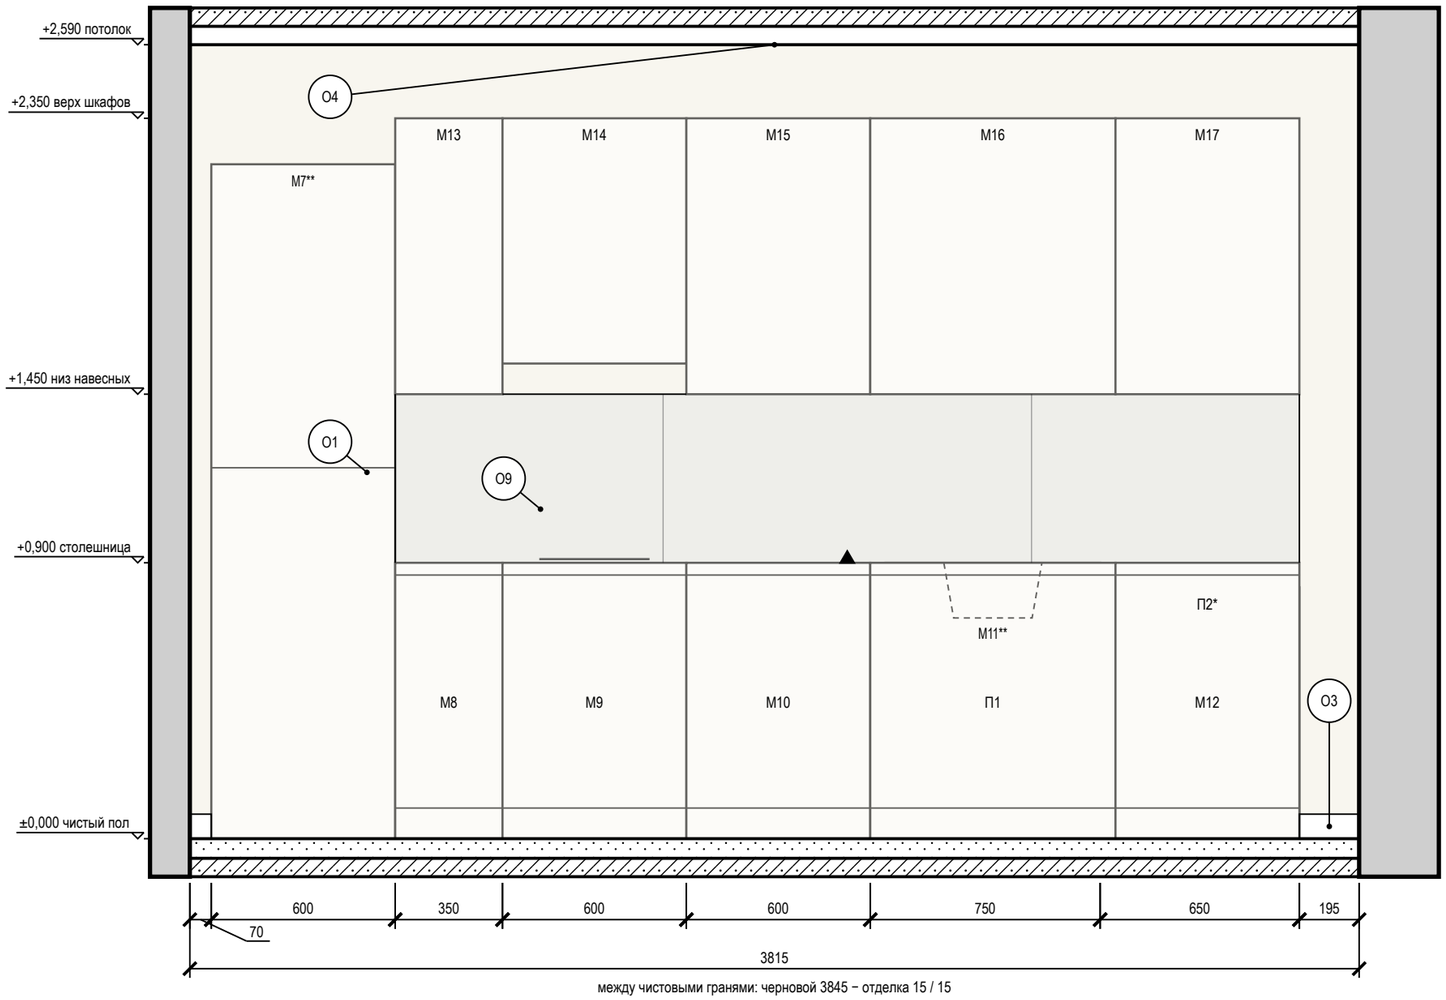

между чистовыми гранями: черновой 3845 − отделка 15 / 15

Схема развёрток (М 1:100)

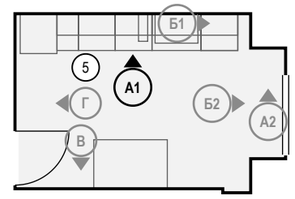

Условные обозначения

- мебель и приборы — фасад по расстановке (условно)
- стены и перекрытия в сечении
- плитка: сетка швов по формату, ▲ — ось старта
- окраска: тон — цвет по коду производителя (условно)
- О1 — марка отделки по реестру отделки альбома
- А — марка развёртки: буква стены, стрелка — взгляд

Ведомость отделки (на листе)

Марка	Поверхность	Материал, изделие	Цвет, код	Кол.
О1	стены	окраска, Farrow & Ball Modern Emulsion, матовая, подготовка Q3	Farrow & Ball No. 2003 «Pointing»	8,3 м²
О3	плинтус	плинтус МДФ, h 80 мм, аналог: плинтус МДФ под покраску 80×16	Farrow & Ball No. 2003 «Pointing»	0,3 м
О4	потолок	окраска, Tikkurila Euro Power 7, глубокоматовая, подготовка Q3	Tikkurila G503 «Calla»	12 м²
О9	фартук	керамогранит, 1200×600×9 мм, аналог: керамогранит под травертин, матовый, затирка CG2WA		1,6 м²

Допущения и предложения на листе

Основа листа: планировка по обводу плана заказчика, не замерена (К-1); высота до плиты 2650 мм от чистого пола — решение автора (ИЗ-1); отметки плана потолков сдвинуты на -95 мм (+2.745 плана = низ плиты), не замерено (К-2); толщины стен приняты: наружные 260 мм, перегородки 130 мм (К-1); положение стен и проёмов — по брифу без обмера и плана БТИ (К-1); разрешённая мощность 10 кВт принята, ТУ не переданы (К-6); вентканалы приняты, в брифе не заданы (К-5); тип дома, перекрытие и несущие стены не известны — документов нет (К-3); плита электрическая — принята, в брифе не указано (К-6); система заземления TN-C-S принята, ТУ не переданы (К-6); число жильцов 2 принято, в брифе не указано (К-9); подрайон климата не задан — принят не северный (жилые от 2,5 м) (К-26).

Знак «*» — принято, не замерено и не подтверждено (замерить на объекте): К-1: окно пом. 5 (стена Б) — окно: положение, ширина, высота и подоконник приняты по обводу плана заказчика, без обмера, не замерены; дверь пом. 5 (стена Г) — проём принят по обводу плана заказчика, без обмера: положение и ширина сняты с плана, не замерены.

Знак «**» — предложение проектировщика, заказчиком не утверждено (согласовать с заказчиком): К-7: М7, М11.

См. лист открытых вопросов (лист 5, записи К-1, К-3, К-5–К-7, К-9; лист 6, запись К-26).

Примечания

1. Развёртки — вид на стену изнутри помещения, по часовой стрелке; расположение — на схеме листа и на листе 71; размеры — в мм по чистовым поверхностям; отметки — в м от ±0,000; высоты Н — от чистого пола помещения до оси изделия, у декора — до центра.
2. Стена А1 показана двумя видами: здесь — архитектурная развёртка (мебель, отделка, проёмы, высоты), электроточки и выводы ВК с привязками и таблицей — на листе 87 («Привязки»).
3. Схема мебели, приборов и декора не является технической документацией для производства мебели; габариты — по паспортам изделий (* — высота не задана в проекте, показана по типовому изделию).

1000 мм · печать 1:1

Изм.	Кол.уч	Лист	№ док.	Подп.	Дата
Разраб.		Кырлан А.С.			04.11.26
Пров.					
ГИП					
Н. контр.					
Утв.					

ГД-2026-020-АИ

Квартира 68 м², элитный модерн

Общая площадь 68,47* м² · * размеры приняты, не замерены (реестр — л. 5–7, К-1)

Дизайн-проект интерьера

Стадия	Лист	Листов
РП	86	105

Развёртка стены А1. Кухня-столовая (пом. 5), кухонный фронт

М 1:20

Кырлан Александр Сергеевич

выпуск 04.11.2026 № 8be4ef4c81 · стр. 95 из 117

Привязки электроточек и выводов ВК, стена А1. Кухня-столовая (пом. 5)

Кухня-столовая (пом. 5) · вид изнутри помещения · привязки в мм, отметки в м · к развёртке на листе 86

ПРЕДВАРИТЕЛЬНО · не для производства работ · открыто пунктов: 25 (реестр — л. 5–7)

Развёртка стены А1: электроточки и выводы

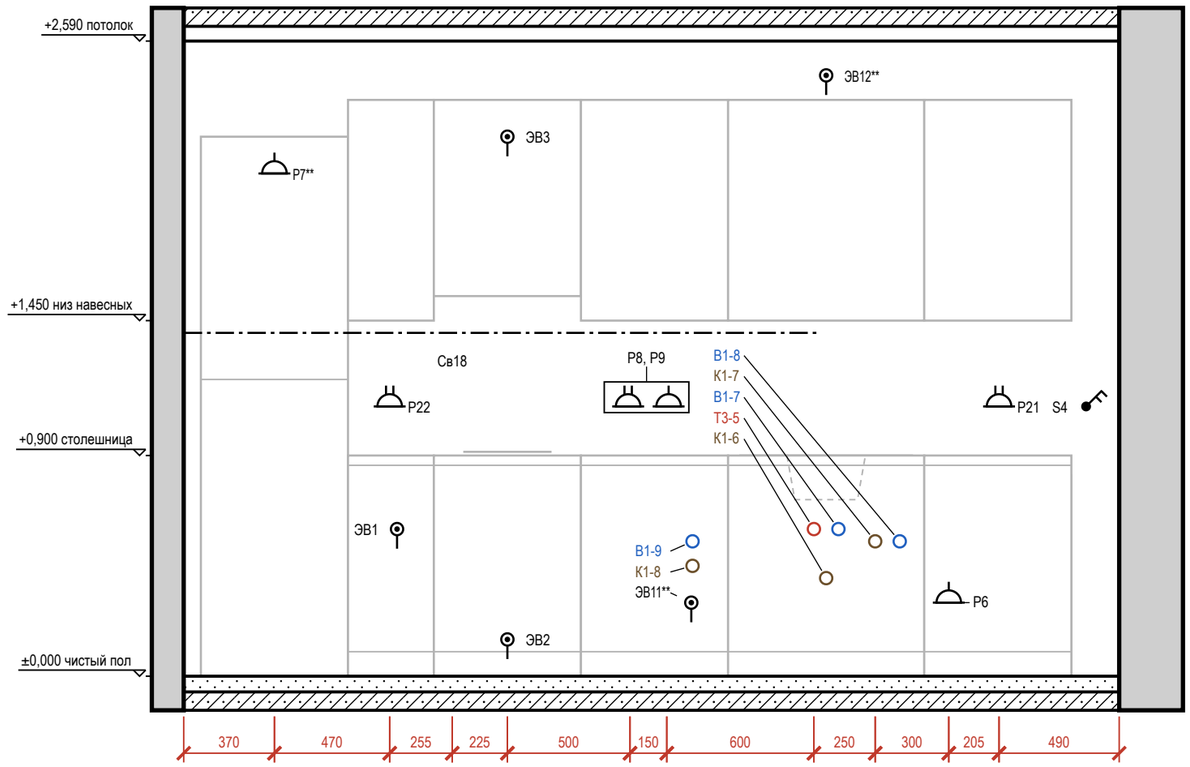



Таблица привязок электроточек и выводов

Марка	Назначение	От угла, мм	Н от пола, мм	Примечание
P7**	розетка: холодильник — над нишей, съёмная панель	370	2050	гр. 10
P22	розетка: фартук	840	1100	рамка 2 поста, гр. 8
ЭВ1	вывод кабеля: варочная панель — в соседнем модуле, за ящиком	870	600	гр. 12
Св18	светильник настенный: марка 13 по исходному плану: «підсвітка робочої поверхні»	1095	1400	гр. 1, лента -405–2595 от угла
ЭВ2	вывод кабеля: духовой шкаф — в цоколе	1320	150	гр. 13
ЭВ3	вывод кабеля: вытяжка — над корпусом	1320	2200	гр. 11
P8	розетка: чайник и кофемашина (отдельная линия)	1820	1100	рамка 2 поста, гр. 9
P9	розетка: фартук: мелкая техника	1970	1100	гр. 8
ЭВ11**	вывод кабеля: измельчитель мойки	2070	300	гр. 8
K1-8	канализация — фильтр обратного осмоса	2075	450	Ø40
B1-9	холодная вода — фильтр обратного осмоса	2075	550	
T3-5	горячая вода — мойка кухонная	2570	600	межос. 100
K1-6	канализация — мойка кухонная	2620	400	Ø50
ЭВ12**	вывод кабеля: подсветка навесных шкафов (блок питания ленты)	2620	2450	гр. 8
B1-7	холодная вода — мойка кухонная	2670	600	межос. 100
K1-7	канализация — посудомоечная машина	2820	550	Ø40; слив ПММ в шкафу мойки
B1-8	холодная вода — посудомоечная машина	2920	550	кран ПММ в шкафу мойки
P6	розетка: посудомоечная машина (в нише М12, сбоку от корпуса, доступ через цоколь)	3120	300	гр. 14
P21	розетка: фартук	3325	1100	рамка 2 поста, гр. 8
S4	выключатель	3680	1100	гр. 1

Условные обозначения

- розетка с заземляющим контактом; у знака — марка, ×N постов в рамке, гр. — группа щита, Н — высота оси, мм
- вывод кабеля для подключения прибора (без розетки), марка ЭВ
- выключатель одноклавишный
- выключатель двухклавишный (флажков — по числу клавиш)
- светодиодная лента в профиле / в карнизе короба
- вывод В1 (код — в ведомости привязок)
- вывод Т3 (код — в ведомости привязок)
- вывод К1 (код — в ведомости привязок)
- привязки точек и выводов от угла и от пола, мм
- А — марка развёртки: буква стены, стрелка — взгляд

Схема развёрток (М 1:200)

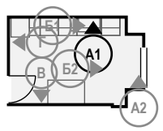

Примечания

1. Вид «Привязки» стены А1 — электроточки и выводы ВК; архитектурная развёртка (мебель, отделка, проёмы, высоты) — на листе 86, расположение — на листе 71. Мебель и приборы — подложкой для ориентира; их марки и обозначения мебели, проёмов и стен — там же.
2. Привязки — в мм: по горизонтали от левого чистового угла стены до оси изделия, Н — от чистого пола до оси; все точки — в таблице привязок. Красная цепочка — привязки по осям; точки ближе 150 мм одна к другой в цепочку не дробятся — их привязки только в таблице.
3. У знака — марка электроточки (Р — розетка, S — выключатель, Св — светильник, ЭВ — вывод кабеля); посты в рамке и группа щита — в графе «Примечание»; группы по клавишам выключателя — на листе выключателей.
4. Коды выводов ВК: В1 — холодная вода, Т3 — горячая вода, К1 — канализация; номер после дефиса — номер вывода на листе выводов сантехники.
5. Выводы кухонной техники — по утверждённому проекту кухни: привязки выводов даются от осей модулей гарнитура.

Допущения и предложения на листе. Основа листа: планировка по обводу плана заказчика, не замерена (К-1); высота до плиты 2650 мм от чистого пола — решение автора (ИЗ-1); отметки плана потолков сдвинуты на -95 мм (+2.745 плана = низ плиты), не замерено (К-2); толщины стен приняты: наружные 260 мм, перегородки 130 мм (К-1); положение стен и проёмов — по брифу без обмера и плана БТИ (К-1); разрешённая мощность 10 кВт принята, ТУ не переданы (К-6); вентканалы приняты, в брифе не заданы (К-5); тип дома, перекрытие и несущие стены не известны — документов нет (К-3); плита электрическая — принята, в брифе не указано (К-6); система заземления TN-C-S принята, ТУ не переданы (К-6); число жильцов 2 принято, в брифе не указано (К-9); подрайон климата не задан — принят не северный (жилые от 2,5 м) (К-26). Знак «*» — принято, не замерено (замерить): К-1: окно пом. 5 (стена Б), дверь пом. 5 (стена Г). Знак «**» — предложено, не утверждено (согласовать): Р7, ЭВ11, ЭВ12. См. лист открытых вопросов (лист 5, записи К-1, К-3, К-5, К-6, К-9; лист 6, запись К-26).

1000 мм · печать 1:1

Изм.	Кол.уч	Лист	№ док.	Подп.	Дата
Разраб.		Кырлан А.С.			04.11.26
Пров.					
ГИП					
Н. контр.					
Утв.					

ГД-2026-020-АИ

Квартира 68 м², элитный модерн

Общая площадь 68,47* м² · * размеры приняты, не замерены (реестр — л. 5–7, К-1)

Дизайн-проект интерьера	Стадия	Лист	Листов
	РП	87	105

Привязки электроточек и выводов ВК, стена А1. Кухня-столовая (пом. 5)

М 1:25

Кырлан Александр Сергеевич


выпуск 04.11.2026 № 8be4ef4c81 · стр. 96 из 117

Развёртки стен А2, Б1, Б2. Кухня-столовая (пом. 5)

Кухня-столовая (пом. 5) · вид изнутри помещения · размеры в мм, отметки в м


ПРЕДВАРИТЕЛЬНО · не для производства работ · открыто пунктов: 25 (реестр — л. 5–7)

Развёртка стены А2

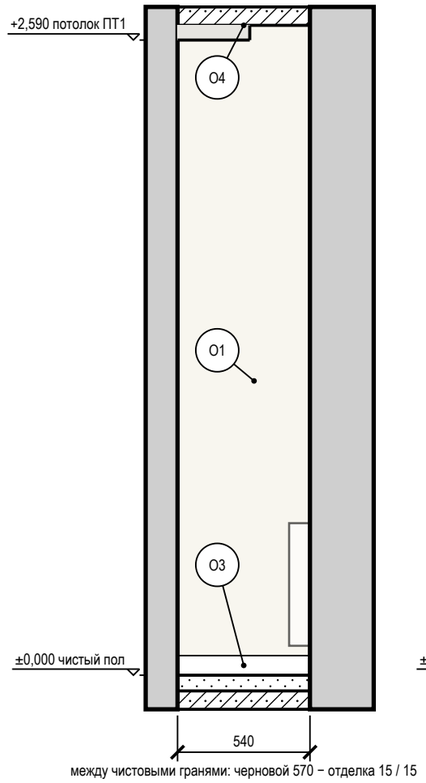


между чистовыми гранями: черновой 570 − отделка 15 / 15

Развёртка стены Б1

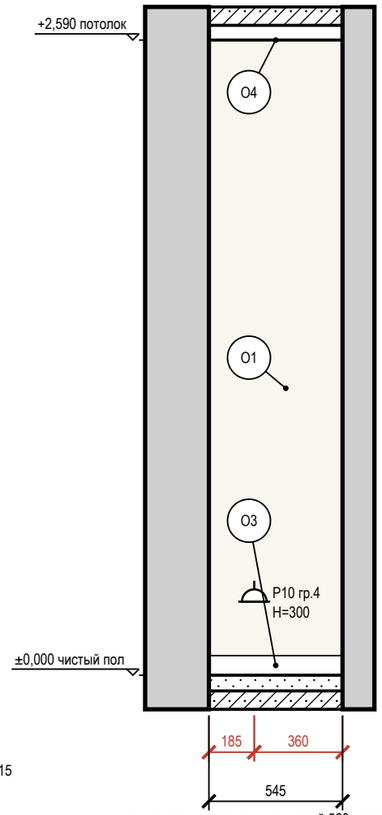


между чистовыми гранями: черновой 560 − отделка 15 / 0

Развёртка стены Б2

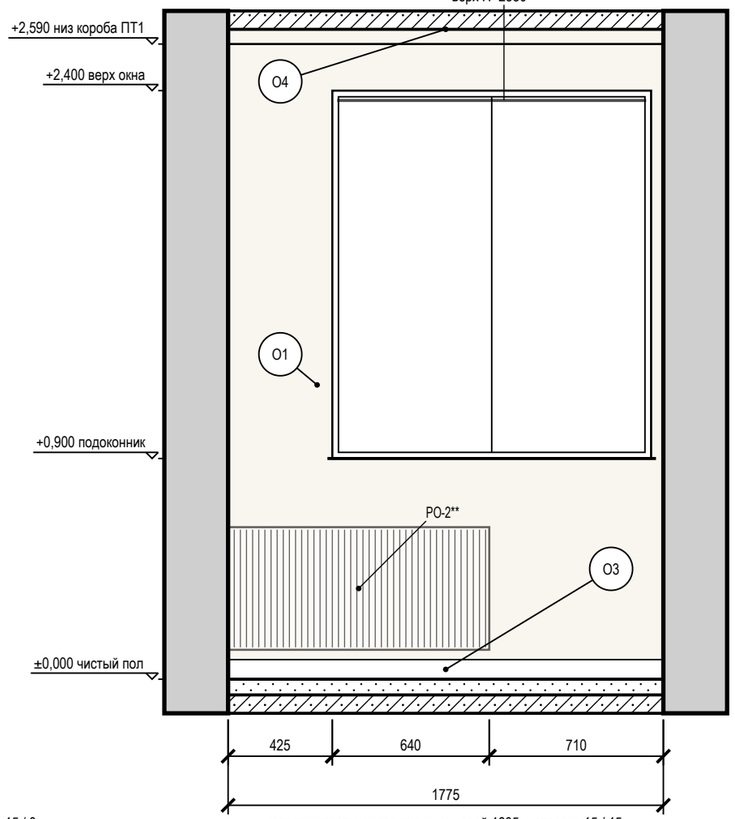

между чистовыми гранями: черновой 1805 − отделка 15 / 15

Схема развёрток (М 1:100)

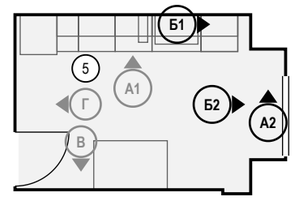

Условные обозначения

- розетка с заземляющим контактом; у знака — марка, ×N постов в рамке, гр. — группа щита, Н — высота оси, мм
- привязки точек и выводов от угла и от пола, мм
- мебель и приборы — фасад по расстановке (условно)
- карниз (шина) и шторы в собранном виде: марка Т, длина L, верх Н
- окно: проём, рама, подоконник
- радиатор отопления; марка — по плану отопления
- стены и перекрытия в сечении
- окраска: тон — цвет по коду производителя (условно)
- О1 — марка отделки по реестру отделки альбома
- А — марка развёртки: буква стены, стрелка — взгляд

Ведомость отделки (на листе)

Марка	Поверхность	Материал, изделие	Цвет, код	Кол.
О1	стены	окраска, Farrow & Ball Modern Emulsion, матовая, подготовка Q3	Farrow & Ball No. 2003 «Pointing»	5,6 м²
О3	плинтус	плинтус МДФ, h 80 мм, аналог: плинтус МДФ под покраску 80×16	Farrow & Ball No. 2003 «Pointing»	2,9 м
О4	потолок	окраска, Tikkurila Euro Power 7, глубокоматовая, подготовка Q3	Tikkurila G503 «Calla»	12 м²

Допущения и предложения на листе

Основа листа: планировка по обводу плана заказчика, не замерена (К-1); высота до плиты 2650 мм от чистого пола — решение автора (ИЗ-1); отметки плана потолков сдвинуты на -95 мм (+2.745 плана = низ плиты), не замерено (К-2); толщины стен приняты: наружные 260 мм, перегородки 130 мм (К-1); положение стен и проёмов — по брифу без обмера и плана БТИ (К-1); разрешённая мощность 10 кВт принята, ТУ не переданы (К-6); вентканалы приняты, в брифе не заданы (К-5); тип дома, перекрытие и несущие стены не известны — документов нет (К-3); плита электрическая — принята, в брифе не указано (К-6); система заземления TN-C-S принята, ТУ не переданы (К-6); число жильцов 2 принято, в брифе не указано (К-9); подрайон климата не задан — принят не северный (жилые от 2,5 м) (К-26).

Знак «*» — принято, не замерено и не подтверждено (замерить на объекте): К-1: окно пом. 5 (стена Б) — окно: положение, ширина, высота и подоконник приняты по обводу плана заказчика, без обмера, не замерены; дверь пом. 5 (стена Г) — проём принят по обводу плана заказчика, без обмера: положение и ширина сняты с плана, не замерены.

Знак «**» — предложение проектировщика, заказчиком не утверждено (согласовать с заказчиком): РО-2 — подключение боковое, воздухоотводчик Маевского и термоголовка — типовое решение для панельного 22; тип подключения зависит от стояка и модели радиатора (запись реестра К-4: положение стояков).

См. лист открытых вопросов (лист 5, записи К-1, К-3, К-5, К-6, К-9; лист 6, запись К-26).

Примечания

1. Развёртки — вид на стену изнутри помещения, по часовой стрелке; расположение — на схеме листа и на листе 71; размеры — в мм по чистовым поверхностям; отметки — в м от ±0,000; высоты Н — от чистого пола помещения до оси изделия, у декора — до центра.
2. Красная цепочка — привязки электроточек и выводов по осям от угла чистовых стен; высота Н — у знака, от чистого пола до оси; высоты мебели, проёмов и границ отделки — колонкой отметок слева. Стена с 5 и более точками или с мелкими звеньями привязок показана двумя видами: архитектурная развёртка (мебель, отделка, проёмы, высоты) и вид «Привязки» на отдельном листе — точки и выводы с марками, одна цепочка по осям и таблица привязок (каждая точка — строка).
3. У знака электроточки: марка (Р — розетка, S — выключатель, Св — светильник, ЭВ — вывод кабеля), ×N — число постов в рамке, гр. — группа щита, Н — высота оси от чистого пола, мм; группы по клавишам выключателя — на листе выключателей.
4. Схема мебели, приборов и декора не является технической документацией для производства мебели; габариты — по паспортам изделий.
5. Карнизы (шины) — по ведомости текстиля декоратора: длина L и верх Н на развёртке — те же числа, что в ведомости; крепление — до окраски потолка.

1000 мм · печать 1:1

Изм.	Кол.уч	Лист	№ док.	Подп.	Дата
Разраб.		Кырлан А.С.			04.11.26
Пров.					
ГИП					
Н. контр.					
Утв.					

ГД-2026-020-АИ

Квартира 68 м², элитный модерн

Общая площадь 68,47* м² · * размеры приняты, не замерены (реестр — л. 5–7, К-1)

Дизайн-проект интерьера

Стадия	Лист	Листов
РП	88	105

Развёртки стен А2, Б1, Б2. Кухня-столовая (пом. 5)

М 1:25

Кырлан Александр Сергеевич


выпуск 04.11.2026 № 8be4ef4c81 · стр. 97 из 117

Развёртки стен В, Г. Кухня-столовая (пом. 5)

Кухня-столовая (пом. 5) · вид изнутри помещения · размеры в мм, отметки в м


ПРЕДВАРИТЕЛЬНО · не для производства работ · открыто пунктов: 25 (реестр — л. 5–7)

Развёртка стены В

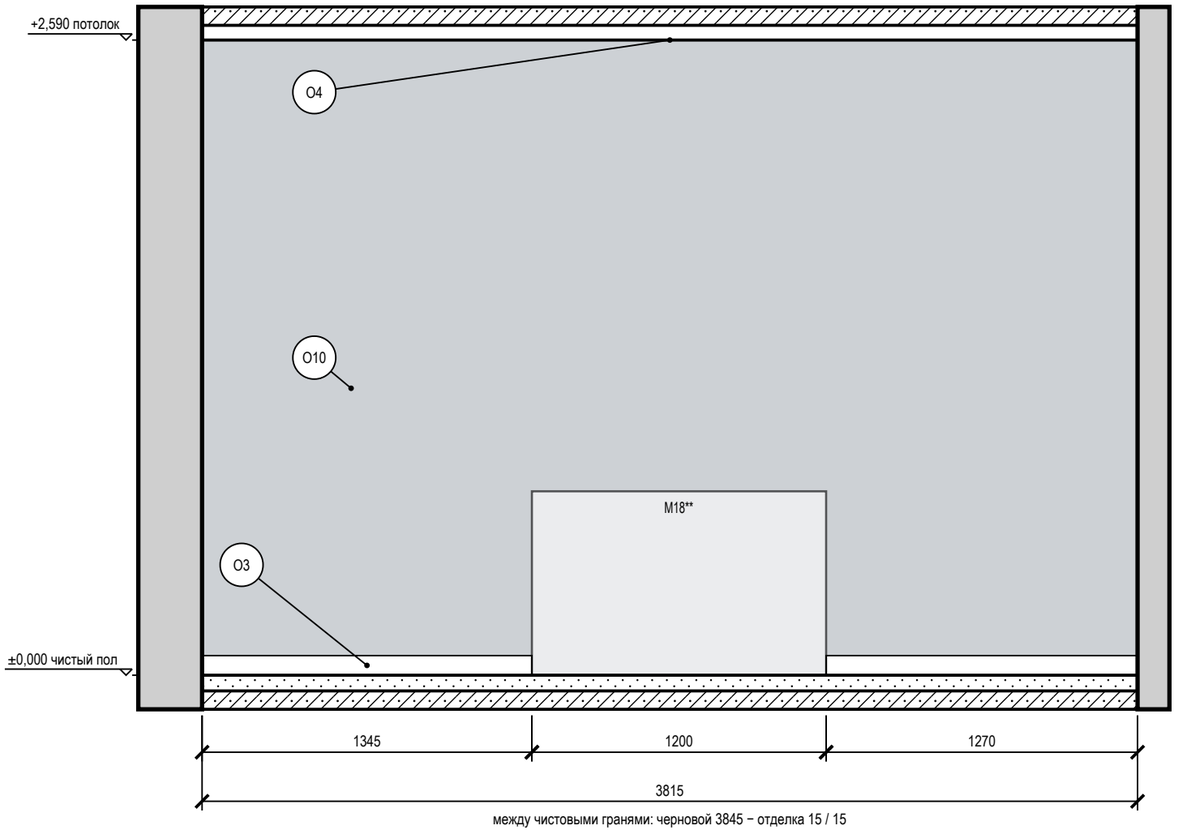


между чистовыми гранями: черновой 3845 − отделка 15 / 15

Развёртка стены Г

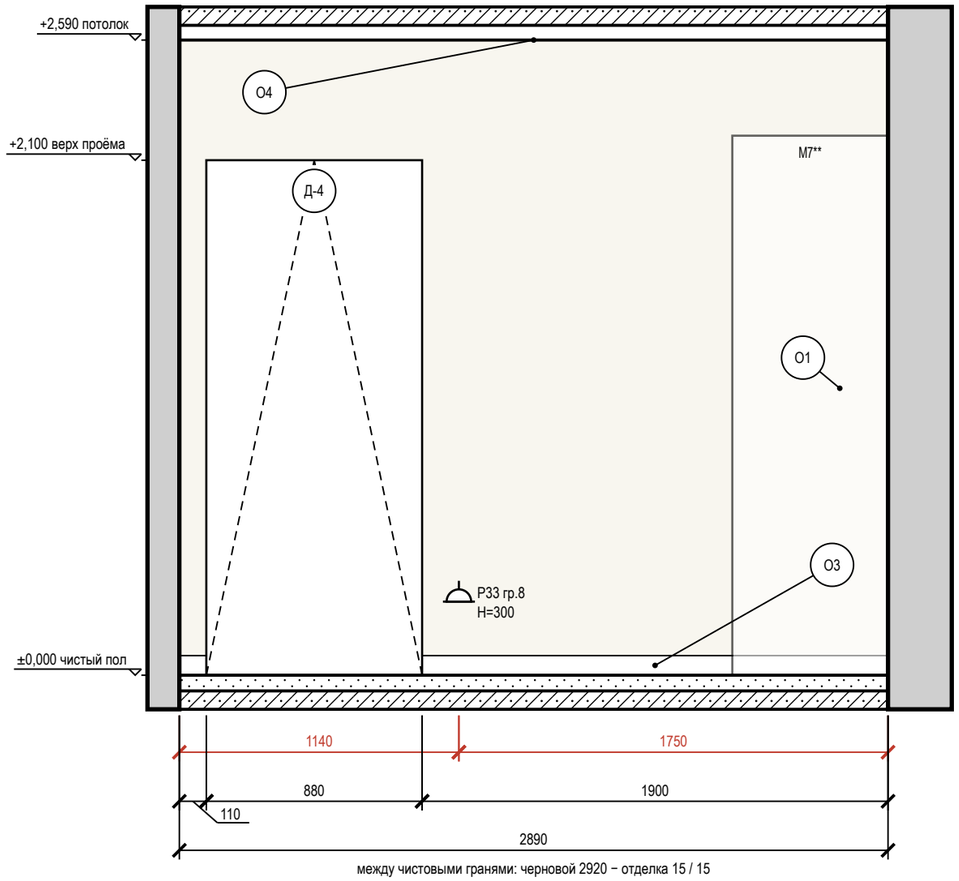

между чистовыми гранями: черновой 2920 − отделка 15 / 15

Схема развёрток (М 1:100)

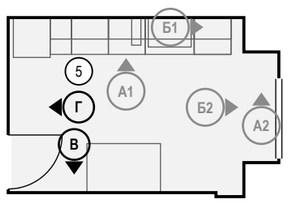

Условные обозначения

- розетка с заземляющим контактом; у знака — марка, ×N постов в рамке, гр. — группа щита, Н — высота оси, мм
- привязки точек и выводов от угла и от пола, мм
- мебель и приборы — фасад по расстановке (условно)
- дверной проём; марка двери — в кружке
- стены и перекрытия в сечении
- окраска: тон — цвет по коду производителя (условно)
- О1 — марка отделки по реестру отделки альбома
- А — марка развёртки: буква стены, стрелка — взгляд

Допущения и предложения на листе

Основа листа: планировка по обводу плана заказчика, не замерена (К-1); высота до плиты 2650 мм от чистого пола — решение автора (ИЗ-1); отметки плана потолков сдвинуты на -95 мм (+2.745 плана = низ плиты), не замерено (К-2); толщины стен приняты: наружные 260 мм, перегородки 130 мм (К-1); положение стен и проёмов — по брифу без обмера и плана БТИ (К-1); разрешённая мощность 10 кВт принята, ТУ не переданы (К-6); вентканалы приняты, в брифе не заданы (К-5); тип дома, перекрытие и несущие стены не известны — документов нет (К-3); плита электрическая — принята, в брифе не указано (К-6); система заземления TN-C-S принята, ТУ не переданы (К-6); число жильцов 2 принято, в брифе не указано (К-9); подрайон климата не задан — принят не северный (жилые от 2,5 м) (К-26).

Знак «*» — принято, не замерено и не подтверждено (замерить на объекте): К-1: окно пом. 5 (стена Б) — окно: положение, ширина, высота и подоконник приняты по обводу плана заказчика, без обмера, не замерены; дверь пом. 5 (стена Г) — проём принят по обводу плана заказчика, без обмера: положение и ширина сняты с плана, не замерены.

Знак «**» — предложение проектировщика, заказчиком не утверждено (согласовать с заказчиком): К-7: М7, М18.

См. лист открытых вопросов (лист 5, записи К-1, К-3, К-5–К-7, К-9; лист 6, запись К-26).

Примечания

1. Развёртки — вид на стену изнутри помещения, по часовой стрелке; расположение — на схеме листа и на листе 71; размеры — в мм по чистовым поверхностям; отметки — в м от ±0,000; высоты Н — от чистого пола помещения до оси изделия, у декора — до центра.
2. Красная цепочка — привязки электроточек и выводов по осям от угла чистовых стен; высота Н — у знака, от чистого пола до оси; высоты мебели, проёмов и границ отделки — колонкой отметок слева. Стена с 5 и более точками или с мелкими звеньями привязок показана двумя видами: архитектурная развёртка (мебель, отделка, проёмы, высоты) и вид «Привязки» на отдельном листе — точки и выводы с марками, одна цепочка по осям и таблица привязок (каждая точка — строка).
3. У знака электроточки: марка (Р — розетка, S — выключатель, Св — светильник, ЭВ — вывод кабеля), ×N — число постов в рамке, гр. — группа щита, Н — высота оси от чистого пола, мм; группы по клавишам выключателя — на листе выключателей.
4. Схема мебели, приборов и декора не является технической документацией для производства мебели; габариты — по паспортам изделий.

1000 мм · печать 1:1

Изм.	Кол.уч	Лист	№ док.	Подп.	Дата
Разраб.		Кырлан А.С.			04.11.26
Пров.					
ГИП					
Н. контр.					
Утв.					

ГД-2026-020-АИ

Квартира 68 м², элитный модерн

Общая площадь 68,47* м² · * размеры приняты, не замерены (реестр — л. 5–7, К-1)

Дизайн-проект интерьера

Стадия	Лист	Листов
РП	89	105

Развёртки стен В, Г. Кухня-столовая (пом. 5)

М 1:25

Кырлан Александр Сергеевич


выпуск 04.11.2026 № 8be4ef4c81 · стр. 98 из 117

Развёртки стен А, Б. Гостиная (пом. 6)

Гостиная (пом. 6) · вид изнутри помещения · размеры в мм, отметки в м


ПРЕДВАРИТЕЛЬНО · не для производства работ · открыто пунктов: 25 (реестр — л. 5–7)

Развёртка стены А

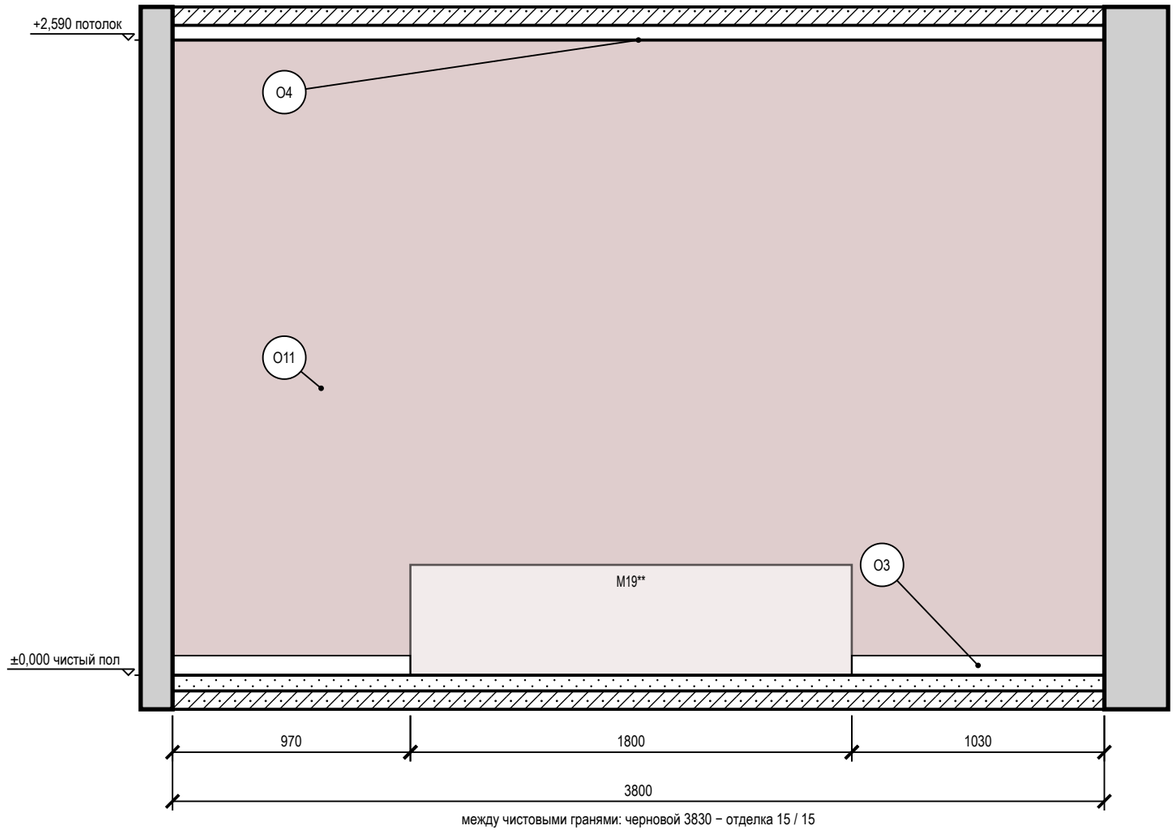


между чистовыми гранями: черновой 3830 − отделка 15 / 15

Развёртка стены Б

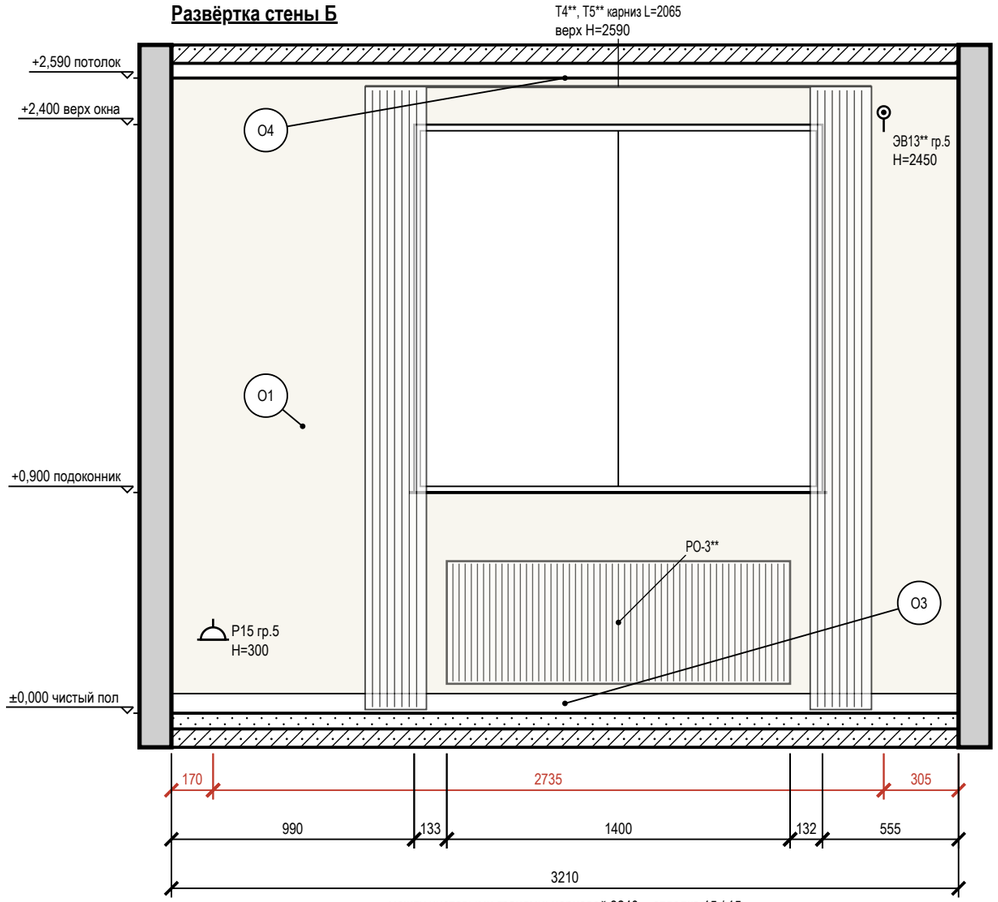

между чистовыми гранями: черновой 3240 − отделка 15 / 15

Схема развёрток (М 1:100)

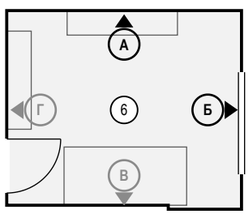

Условные обозначения

- розетка с заземляющим контактом; у знака — марка, ×N постов в рамке, гр. — группа щита, Н — высота оси, мм
- вывод кабеля для подключения прибора (без розетки), марка ЭВ
- привязки точек и выводов от угла и от пола, мм
- мебель и приборы — фасад по расстановке (условно)
- карниз (шина) и шторы в собранном виде: марка Т, длина L, верх Н
- окно: проём, рама, подоконник
- радиатор отопления; марка — по плану отопления
- стены и перекрытия в сечении
- окраска: тон — цвет по коду производителя (условно)
- О1 — марка отделки по реестру отделки альбома
- А — марка развёртки: буква стены, стрелка — взгляд

Допущения и предложения на листе. Основа листа: планировка по обводу плана заказчика, не замерена (К-1); высота до плиты 2650 мм от чистого пола — решение автора (ИЗ-1); отметки плана потолков сдвинуты на -95 мм (+2.745 плана = низ плиты), не замерено (К-2); толщины стен приняты: наружные 260 мм, перегородки 130 мм (К-1); положение стен и проёмов — по брифу без обмера и плана БТИ (К-1); разрешённая мощность 10 кВт принята, ТУ не переданы (К-6); вентканалы приняты, в брифе не заданы (К-5); тип дома, перекрытие и несущие стены не известны — документов нет (К-3); плита электрическая — принята, в брифе не указано (К-6); система заземления TN-C-S принята, ТУ не переданы (К-6); число жильцов 2 принято, в брифе не указано (К-9); подрайон климата не задан — принят не северный (жилые от 2,5 м) (К-26). Знак «*» — принято, не замерено и не подтверждено (замерить на объекте): К-1: окно пом. 6 (стена Б) — окно: положение, ширина, высота и подоконник приняты по обводу плана заказчика, без обмера, не замерены; дверь пом. 6 (стена Г) — проём принят по обводу плана заказчика, без обмера: положение и ширина сняты с плана, не замерены. Знак «**» — предложение проектировщика, заказчиком не утверждено (согласовать с заказчиком): РО-3 — подключение боковое, воздухоотводчик Маевского и термоголовка — типовое решение для панельного 22; тип подключения зависит от стояка и модели радиатора (запись реестра К-4: положение стояков); ЭВ13 — электропривод штор — предложение по умолчанию (комфорт): вывод у окна рядом с карнизом; без привода вывод остаётся резервным, заказчик может снять. См. лист открытых вопросов (лист 5, записи К-1, К-3, К-5–К-7, К-9; лист 6, запись К-26).

Примечания

1. Развёртки — вид на стену изнутри помещения, по часовой стрелке; расположение — на схеме листа и на листе 71; размеры — в мм по чистовым поверхностям; отметки — в м от ±0,000; высоты Н — от чистого пола помещения до оси изделия, у декора — до центра.
2. Красная цепочка — привязки электроточек и выводов по осям от угла чистовых стен; высота Н — у знака, от чистого пола до оси; высоты мебели, проёмов и границ отделки — колонкой отметок слева. Стена с 5 и более точками или с мелкими звеньями привязок показана двумя видами: архитектурная развёртка (мебель, отделка, проёмы, высоты) и вид «Привязки» на отдельном листе — точки и выводы с марками, одна цепочка по осям и таблица привязок (каждая точка — строка).
3. Стена А показана двумя видами: здесь — архитектурная развёртка (мебель, отделка, проёмы, высоты), электроточки и выводы ВК с привязками и таблицей — на листе 91 («Привязки»).
4. У знака электроточки: марка (Р — розетка, S — выключатель, Св — светильник, ЭВ — вывод кабеля), ×N — число постов в рамке, гр. — группа щита, Н — высота оси от чистого пола, мм; группы по клавишам выключателя — на листе выключателей.
5. Схема мебели, приборов и декора не является технической документацией для производства мебели; габариты — по паспортам изделий.
6. Карнизы (шины) — по ведомости текстиля декоратора: длина L и верх Н на развёртке — те же числа, что в ведомости; крепление — до окраски потолка.

1000 мм · печать 1:1

Изм.	Кол.уч	Лист	№ док.	Подп.	Дата
Разраб.		Кырлан А.С.			04.11.26
Пров.					
ГИП					
Н. контр.					
Утв.					

ГД-2026-020-АИ

Квартира 68 м², элитный модерн

Общая площадь 68,47* м² · * размеры приняты, не замерены (реестр — л. 5–7, К-1)

Дизайн-проект интерьера

Стадия	Лист	Листов
РП	90	105

Развёртки стен А, Б. Гостиная (пом. 6)

М 1:25

Кырлан Александр Сергеевич

выпуск 04.11.2026 № 8be4ef4c81 · стр. 99 из 117

Привязки электроточек, стена А. Гостиная (пом. 6)

Гостиная (пом. 6) · вид изнутри помещения · привязки в мм, отметки в м · к развёртке на листе 90

ПРЕДВАРИТЕЛЬНО · не для производства работ · открыто пунктов: 25 (реестр — л. 5–7)

Развёртка стены А: электроточки и выводы

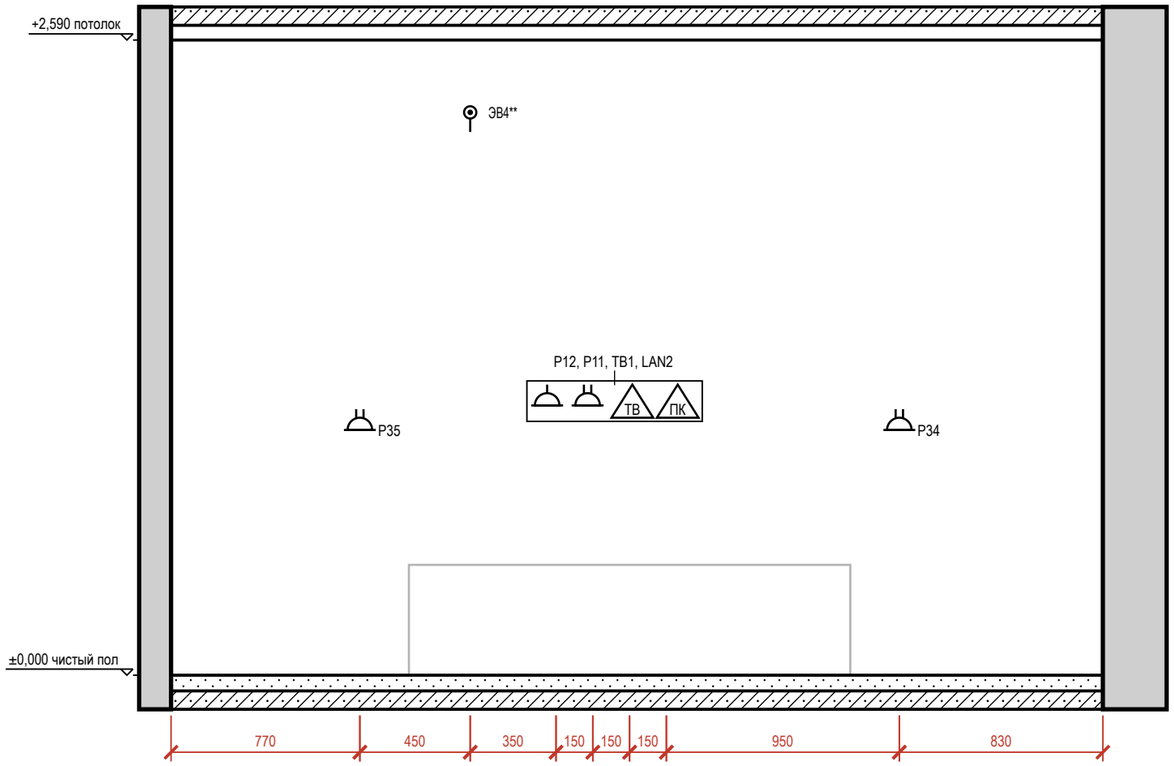



Таблица привязок электроточек и выводов

Марка	Назначение	От угла, мм	Н от пола, мм	Примечание
P35	розетка: ТВ-зона: приставка, консоль, саундбар	770	1000	рамка 2 поста, гр. 5
ЭВ4**	вывод кабеля: кондиционер КВ-1** — вывод питания внутреннего блока	1220	2295	гр. 17
P12	розетка: саундбар	1570	1100	гр. 5
P11	розетка: ТВ, приставка	1720	1100	рамка 2 поста, гр. 5
TB1	розетка ТВ: ТВ-зона	1870	1100	
LAN2	розетка RJ45: Smart TV	2020	1100	
P34	розетка: ТВ-зона: приставка, консоль, саундбар	2970	1000	рамка 2 поста, гр. 5

Условные обозначения

- розетка с заземляющим контактом; у знака — марка, ×N постов в рамке, гр. — группа щита, Н — высота оси, мм
- вывод кабеля для подключения прибора (без розетки), марка ЭВ
- ПК — розетка компьютерная RJ45
- ТВ — розетка телевизионная
- привязки точек и выводов от угла и от пола, мм
- A — марка развёртки: буква стены, стрелка — взгляд

Схема развёрток (М 1:100)

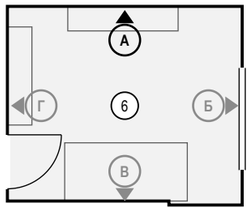

Допущения и предложения на листе

Основа листа: планировка по обводу плана заказчика, не замерена (К-1); высота до плиты 2650 мм от чистого пола — решение автора (ИЗ-1); отметки плана потолков сдвинуты на -95 мм (+2.745 плана = низ плиты), не замерено (К-2); толщины стен приняты: наружные 260 мм, перегородки 130 мм (К-1); положение стен и проёмов — по брифу без обмера и плана БТИ (К-1); разрешённая мощность 10 кВт принята, ТУ не переданы (К-6); вентканалы приняты, в брифе не заданы (К-5); тип дома, перекрытие и несущие стены не известны — документов нет (К-3); плита электрическая — принята, в брифе не указано (К-6); система заземления TN-C-S принята, ТУ не переданы (К-6); число жильцов 2 принято, в брифе не указано (К-9); подрайон климата не задан — принят не северный (жилые от 2,5 м) (К-26).

Знак «*» — принято, не замерено и не подтверждено (замерить на объекте): К-1: окно пом. 6 (стена Б) — окно: положение, ширина, высота и подоконник приняты по обводу плана заказчика, без обмера, не замерены; дверь пом. 6 (стена Г) — проём принят по обводу плана заказчика, без обмера: положение и ширина сняты с плана, не замерены.

Знак «**» — предложение проектировщика, заказчиком не утверждено (согласовать с заказчиком): КВ-1 — кондиционер в жилой комнате — предложение по умолчанию (комфорт), заказчик может снять; модель, наружный блок, трасса фреона и дренаж — после обмера и согласования фасада; ЭВ4 — питание внутреннего блока КВ-1: отдельная линия С16, вывод рядом с блоком под потолком.

См. лист открытых вопросов (лист 5, записи К-1, К-3, К-5, К-6, К-9; лист 6, запись К-26).

Примечания

1. Вид «Привязки» стены А — электроточки и выводы ВК; архитектурная развёртка (мебель, отделка, проёмы, высоты) — на листе 90, расположение — на листе 71. Мебель и приборы — подложкой для ориентира; их марки и обозначения мебели, проёмов и стен — там же.
2. Привязки — в мм: по горизонтали от левого чистового угла стены до оси изделия, Н — от чистого пола до оси; все точки — в таблице привязок. Красная цепочка — привязки по осям; точки ближе 150 мм одна к другой в цепочку не дробятся — их привязки только в таблице.
3. У знака — марка электроточки (Р — розетка, S — выключатель, Св — светильник, ЭВ — вывод кабеля); посты в рамке и группа щита — в графе «Примечание»; группы по клавишам выключателя — на листе выключателей.

1000 мм · печать 1:1

Изм.	Кол.уч	Лист	№ док.	Подп.	Дата
Разраб.		Кырлан А.С.			04.11.26
Пров.					
ГИП					
Н. контр.					
Утв.					

ГД-2026-020-АИ

Квартира 68 м², элитный модерн

Общая площадь 68,47* м² · * размеры приняты, не замерены (реестр — л. 5–7, К-1)

Дизайн-проект интерьера

Стадия	Лист	Листов
РП	91	105

Привязки электроточек, стена А. Гостиная (пом. 6)

М 1:25

Кырлан Александр Сергеевич


выпуск 04.11.2026 № 8be4ef4c81 · стр. 100 из 117

Развёртки стен В, Г. Гостиная (пом. 6)

Гостиная (пом. 6) · вид изнутри помещения · размеры в мм, отметки в м


ПРЕДВАРИТЕЛЬНО · не для производства работ · открыто пунктов: 25 (реестр — л. 5–7)

Развёртка стены В

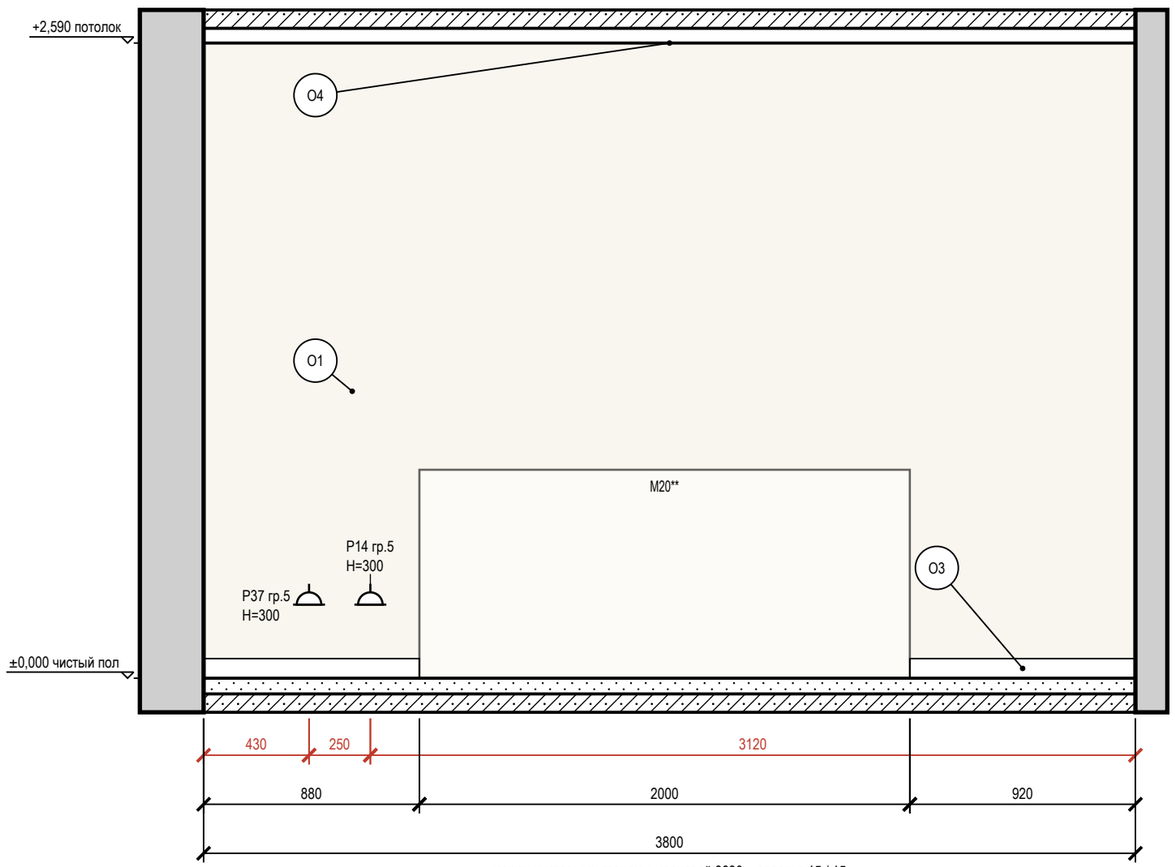


между чистовыми гранями: черновой 3830 − отделка 15 / 15

Развёртка стены Г

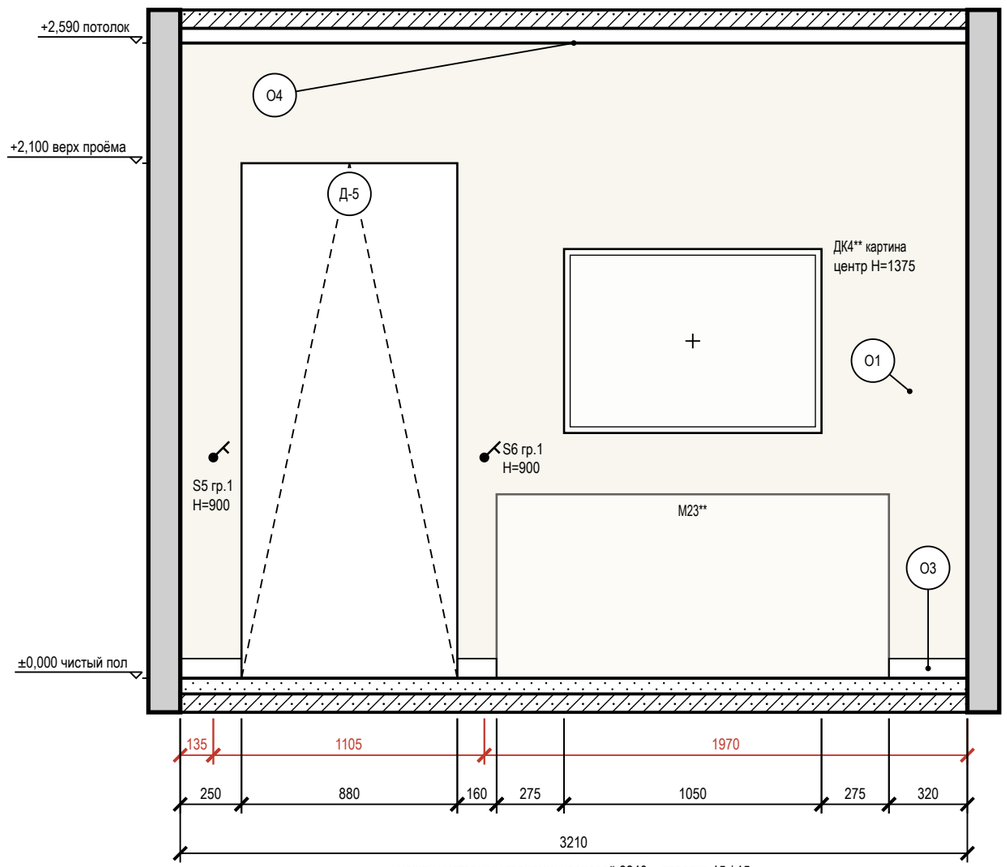

между чистовыми гранями: черновой 3240 − отделка 15 / 15

Схема развёрток (М 1:100)

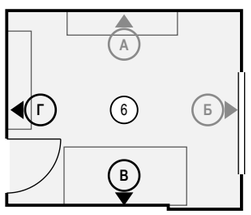

Условные обозначения

- розетка с заземляющим контактом; у знака — марка, ×N постов в рамке, гр. — группа щита, H — высота оси, мм
- выключатель одноклавишный
- привязки точек и выводов от угла и от пола, мм
- мебель и приборы — фасад по расстановке (условно)
- картина (декор): марка Д, крест — центр, H — высота центра, мм
- дверной проём; марка двери — в кружке
- стены и перекрытия в сечении
- окраска: тон — цвет по коду производителя (условно)
- О1 — марка отделки по реестру отделки альбома
- А — марка развёртки: буква стены, стрелка — взгляд

Ведомость отделки (на листе)

Марка	Поверхность	Материал, изделие	Цвет, код	Кол.
О1	стены	окраска, Farrow & Ball Modern Emulsion, матовая, подготовка Q3	Farrow & Ball No. 2003 «Pointing»	16,3 м²
О3	плинтус	плинтус МДФ, h 80 мм, аналог: плинтус МДФ под покраску 80×16	Farrow & Ball No. 2003 «Pointing»	2,5 м
О4	потолок	окраска, Tikkurila Euro Power 7, глубокоматовая, подготовка Q3	Tikkurila G503 «Calla»	12,2 м²

Примечания

1. Развёртки — вид на стену изнутри помещения, по часовой стрелке; расположение — на схеме листа и на листе 71; размеры — в мм по чистовым поверхностям; отметки — в м от ±0,000; высоты H — от чистого пола помещения до оси изделия, у декора — до центра.
2. Красная цепочка — привязки электроточек и выводов по осям от угла чистовых стен; высота H — у знака, от чистого пола до оси; высоты мебели, проёмов и границ отделки — колонкой отметок слева. Стена с 5 и более точками или с мелкими звеньями привязок показана двумя видами: архитектурная развёртка (мебель, отделка, проёмы, высоты) и вид «Привязки» на отдельном листе — точки и выводы с марками, одна цепочка по осям и таблица привязок (каждая точка — строка).
3. У знака электроточки: марка (Р — розетка, S — выключатель, Св — светильник, ЭВ — вывод кабеля), ×N — число постов в рамке, гр. — группа щита, H — высота оси от чистого пола, мм; группы по клавишам выключателя — на листе выключателей.
4. Схема мебели, приборов и декора не является технической документацией для производства мебели; габариты — по паспортам изделий.
5. Картины и зеркала крепить к основанию по паспорту изделия (закладные и анкеры — в перечне скрытых работ); крест — ось центра предмета.

Допущения и предложения на листе. Знак «*» принято (замерить): окно пом. 6 (стена Б), дверь пом. 6 (стена Г). Знак «**» предложено (согласовать). См. лист открытых вопросов (листы 5–7).

1000 мм · печать 1:1

Изм.	Кол.уч	Лист	№ док.	Подп.	Дата
Разраб.		Кырлан А.С.			04.11.26
Пров.					
ГИП					
Н. контр.					
Утв.					

ГД-2026-020-АИ

Квартира 68 м², элитный модерн

Общая площадь 68,47* м² · * размеры приняты, не замерены (реестр — л. 5–7, К-1)

Дизайн-проект интерьера

Стадия	Лист	Листов
РП	92	105

Развёртки стен В, Г. Гостиная (пом. 6)

М 1:25

Кырлан Александр Сергеевич


выпуск 04.11.2026 № 8be4ef4c81 · стр. 101 из 117

Развёртки стен А1, А2. Спальня (пом. 7)

Спальня (пом. 7) · вид изнутри помещения · размеры в мм, отметки в м


ПРЕДВАРИТЕЛЬНО · не для производства работ · открыто пунктов: 25 (реестр — л. 5–7)

Развёртка стены А1

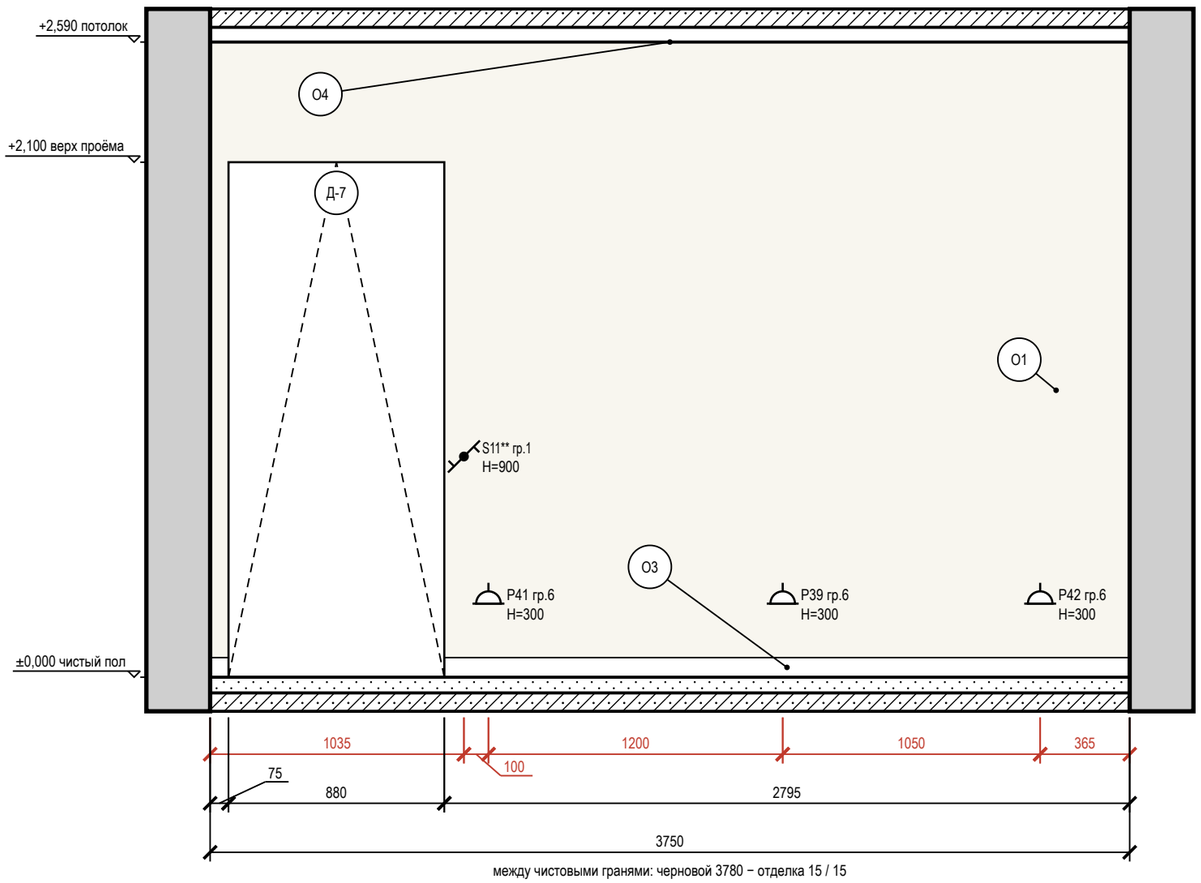

между чистовыми гранями: черновой 3780 − отделка 15 / 15

Развёртка стены А2

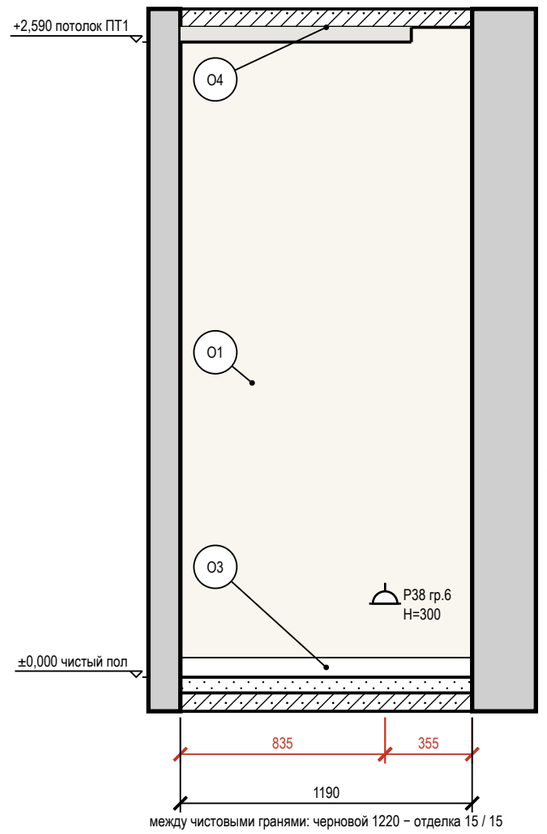

между чистовыми гранями: черновой 1220 − отделка 15 / 15

Условные обозначения

- розетка с заземляющим контактом; у знака — марка, ×N постов в рамке, гр. — группа щита, Н — высота оси, мм
- выключатель одноклавишный
- выключатель с проходной или перекрёстной клавишей (обратный флажок); тип клавиши — в подписи
- привязки точек и выводов от угла и от пола, мм
- мебель и приборы — фасад по расстановке (условно)
- дверной проём; марка двери — в кружке
- стены и перекрытия в сечении
- окраска: тон — цвет по коду производителя (условно)
- О1 — марка отделки по реестру отделки альбома
- А — марка развёртки: буква стены, стрелка — взгляд

Допущения и предложения на листе


Основа листа: планировка по обводу плана заказчика, не замерена (К-1); высота до плиты 2650 мм от чистого пола — решение автора (ИЗ-1); отметки плана потолков сдвинуты на -95 мм (+2.745 плана = низ плиты), не замерено (К-2); толщины стен приняты: наружные 260 мм, перегородки 130 мм (К-1); положение стен и проёмов — по брифу без обмера и плана БТИ (К-1); разрешённая мощность 10 кВт принята, ТУ не переданы (К-6); вентканалы приняты, в брифе не заданы (К-5); тип дома, перекрытие и несущие стены не известны — документов нет (К-3); плита электрическая — принята, в брифе не указано (К-6); система заземления TN-C-S принята, ТУ не переданы (К-6); число жильцов 2 принято, в брифе не указано (К-9); подрайон климата не задан — принят не северный (жилые от 2,5 м) (К-26).

Знак «*» — принято, не замерено и не подтверждено (замерить на объекте): К-1: окно пом. 7 (стена Б) — окно: положение, ширина, высота и подоконник приняты по обводу плана заказчика, без обмера, не замерены; дверь пом. 7 (стена А) — проём принят по обводу плана заказчика, без обмера: положение и ширина сняты с плана, не замерены.

Знак «**» — предложение проектировщика, заказчиком не утверждено (согласовать с заказчиком): S11 — у входа в спальню нужен выключатель основного света 08-А/08-Б, прикроватные — проходные.

См. лист открытых вопросов (лист 5, записи К-1, К-3, К-5, К-6, К-9; лист 6, запись К-26).

Схема развёрток (М 1:100)

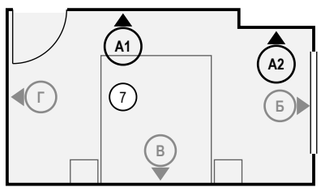

Ведомость отделки (на листе)

Марка	Поверхность	Материал, изделие	Цвет, код	Кол.
О1	стены	окраска, Farrow & Ball Modern Emulsion, матовая, подготовка Q3	Farrow & Ball No. 2003 «Pointing»	11 м²
О3	плинтус	плинтус МДФ, h 80 мм, аналог: плинтус МДФ под покраску 80×16	Farrow & Ball No. 2003 «Pointing»	4,1 м
О4	потолок	окраска, Tikkurila Euro Power 7, глубокоматовая, подготовка Q3	Tikkurila G503 «Calla»	13,9 м²

Примечания

1. Развёртки — вид на стену изнутри помещения, по часовой стрелке; расположение — на схеме листа и на листе 71; размеры — в мм по чистовым поверхностям; отметки — в м от ±0,000; высоты Н — от чистого пола помещения до оси изделия, у декора — до центра.
2. Красная цепочка — привязки электроточек и выводов по осям от угла чистовых стен; высота Н — у знака, от чистого пола до оси; высоты мебели, проёмов и границ отделки — колонкой отметок слева. Стена с 5 и более точками или с мелкими звеньями привязок показана двумя видами: архитектурная развёртка (мебель, отделка, проёмы, высоты) и вид «Привязки» на отдельном листе — точки и выводы с марками, одна цепочка по осям и таблица привязок (каждая точка — строка).
3. У знака электроточки: марка (Р — розетка, S — выключатель, Св — светильник, ЭВ — вывод кабеля), ×N — число постов в рамке, гр. — группа щита, Н — высота оси от чистого пола, мм; группы по клавишам выключателя — на листе выключателей.
4. Схема мебели, приборов и декора не является технической документацией для производства мебели; габариты — по паспортам изделий.

1000 мм · печать 1:1

Изм.	Кол.уч	Лист	№ док.	Подп.	Дата
Разраб.		Кырлан А.С.			04.11.26
Пров.					
ГИП					
Н. контр.					
Утв.					

ГД-2026-020-АИ

Квартира 68 м², элитный модерн

Общая площадь 68,47* м² · * размеры приняты, не замерены (реестр — л. 5–7, К-1)

Дизайн-проект интерьера

Стадия	Лист	Листов
РП	93	105

Развёртки стен А1, А2. Спальня (пом. 7)

М 1:25

Кырлан Александр Сергеевич


выпуск 04.11.2026 № 8be4ef4c81 · стр. 102 из 117

Развёртка стены Б. Спальня (пом. 7)

Спальня (пом. 7) · вид изнутри помещения · размеры в мм, отметки в м

ПРЕДВАРИТЕЛЬНО · не для производства работ · открыто пунктов: 25 (реестр — л. 5–7)

Развёртка стены Б

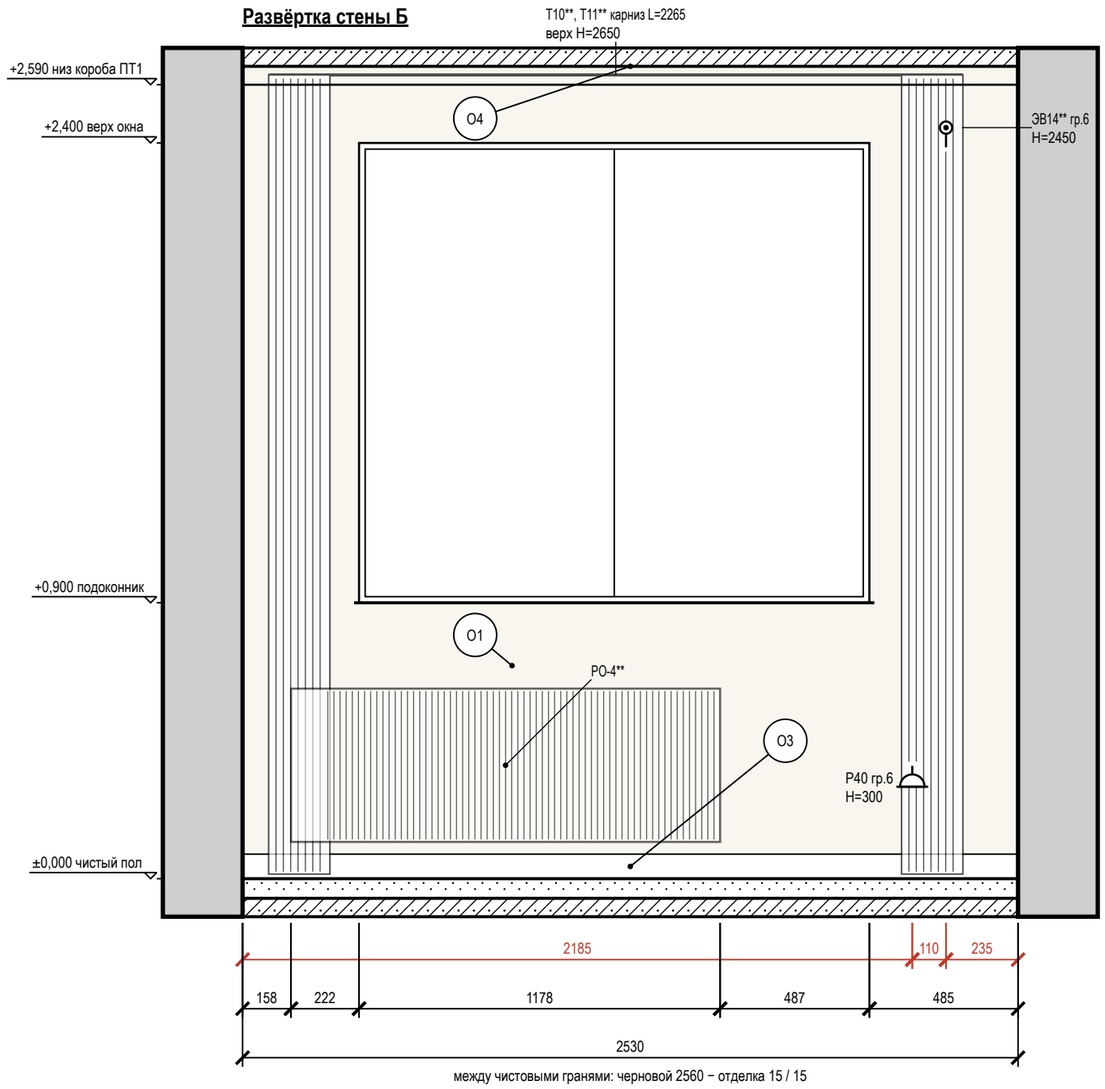

между чистовыми гранями: черновой 2560 − отделка 15 / 15


Допущения и предложения на листе. Основа листа: планировка по обводу плана заказчика, не замерена (К-1); высота до плиты 2650 мм от чистого пола — решение автора (ИЗ-1); отметки плана потолков сдвинуты на -95 мм (+2.745 плана = низ плиты), не замерено (К-2); толщины стен приняты: наружные 260 мм, перегородки 130 мм (К-1); положение стен и проёмов — по брифу без обмера и плана БТИ (К-1); разрешённая мощность 10 кВт принята, ТУ не переданы (К-6); вентканалы приняты, в брифе не заданы (К-5); тип дома, перекрытие и несущие стены не известны — документов нет (К-3); плита электрическая — принята, в брифе не указано (К-6); система заземления TN-C-S принята, ТУ не переданы (К-6); число жильцов 2 принято, в брифе не указано (К-9); подрайон климата не задан — принят не северный (жилые от 2,5 м) (К-26). Знак «*» — принято, не замерено и не подтверждено (замерить на объекте): К-1: окно пом. 7 (стена Б) — окно: положение, ширина, высота и подоконник приняты по обводу плана заказчика, без обмера, не замерены; дверь пом. 7 (стена А) — проём принят по обводу плана заказчика, без обмера: положение и ширина сняты с плана, не замерены. Знак «**» — предложение проектировщика, заказчиком не утверждено (согласовать с заказчиком): РО-4 — подключение боковое, воздухоотводчик Маевского и термоголовка — типовое решение для панельного 22; тип подключения зависит от стояка и модели радиатора (запись реестра К-4: положение стояков); ЭВ14 — электропривод штор — предложение по умолчанию (комфорт): вывод у окна рядом с карнизом; без привода вывод остаётся резервным, заказчик может снять. См. лист открытых вопросов (лист 5, записи К-1, К-3, К-5–К-7, К-9; лист 6, запись К-26).

Примечания

1. Развёртки — вид на стену изнутри помещения, по часовой стрелке; расположение — на схеме листа и на листе 71; размеры — в мм по чистовым поверхностям; отметки — в м от ±0,000; высоты H — от чистого пола помещения до оси изделия, у декора — до центра.
2. Красная цепочка — привязки электроточек и выводов по осям от угла чистовых стен; высота H — у знака, от чистого пола до оси; высоты мебели, проёмов и границ отделки — колонкой отметок слева. Стена с 5 и более точками или с мелкими звеньями привязок показана двумя видами: архитектурная развёртка (мебель, отделка, проёмы, высоты) и вид «Привязки» на отдельном листе — точки и выводы с марками, одна цепочка по осям и таблица привязок (каждая точка — строка).
3. У знака электроточки: марка (Р — розетка, S — выключатель, Св — светильник, ЭВ — вывод кабеля), ×N — число постов в рамке, гр. — группа щита, H — высота оси от чистого пола, мм; группы по клавишам выключателя — на листе выключателей.
4. Схема мебели, приборов и декора не является технической документацией для производства мебели; габариты — по паспортам изделий.
5. Карнизы (шины) — по ведомости текстиля декоратора: длина L и верх H на развёртке — те же числа, что в ведомости; крепление — до окраски потолка.
6. Линии узора (швы плитки, складки штор, рёбра радиаторов) прерываются у знаков и выносок — просвет между линиями не менее 0,7 мм.

1000 мм · печать 1:1

Схема развёрток (М 1:100)

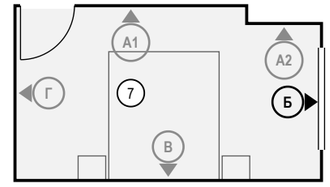

Условные обозначения

- розетка с заземляющим контактом; у знака — марка, ×N постов в рамке, гр. — группа щита, H — высота оси, мм
- вывод кабеля для подключения прибора (без розетки), марка ЭВ
- привязки точек и выводов от угла и от пола, мм
- мебель и приборы — фасад по расстановке (условно)
- карниз (шина) и шторы в собранном виде: марка Т, длина L, верх H
- окно: проём, рама, подоконник
- радиатор отопления; марка — по плану отопления
- стены и перекрытия в сечении
- окраска: тон — цвет по коду производителя (условно)
- О1 — марка отделки по реестру отделки альбома
- А — марка развёртки: буква стены, стрелка — взгляд

Ведомость отделки (на листе)

Марка	Поверхность	Материал, изделие	Цвет, код	Кол.
О1	стены	окраска, Farrow & Ball Modern Emulsion, матовая, подготовка Q3	Farrow & Ball No. 2003 «Pointing»	4,2 м²
О3	плинтус	плинтус МДФ, h 80 мм, аналог: плинтус МДФ под покраску 80×16	Farrow & Ball No. 2003 «Pointing»	2,5 м
О4	потолок	окраска, Tikkurila Euro Power 7, глубокоматовая, подготовка Q3	Tikkurila G503 «Calla»	13,9 м²

Изм.	Кол.уч	Лист	№ док.	Подп.	Дата
Разраб.		Кырлан А.С.			04.11.26
Пров.					
ГИП					
Н. контр.					
Утв.					

ГД-2026-020-АИ

Квартира 68 м², элитный модерн

Общая площадь 68,47* м² · * размеры приняты, не замерены (реестр — л. 5–7, К-1)

Дизайн-проект интерьера

Стадия	Лист	Листов
РП	94	105

Развёртка стены Б. Спальня (пом. 7)

М 1:20

Кырлан Александр Сергеевич


выпуск 04.11.2026 № 8be4ef4c81 · стр. 103 из 117

Развёртка стены В. Спальня (пом. 7)

Спальня (пом. 7) · вид изнутри помещения · размеры в мм, отметки в м


ПРЕДВАРИТЕЛЬНО · не для производства работ · открыто пунктов: 25 (реестр — л. 5–7)

Развёртка стены В

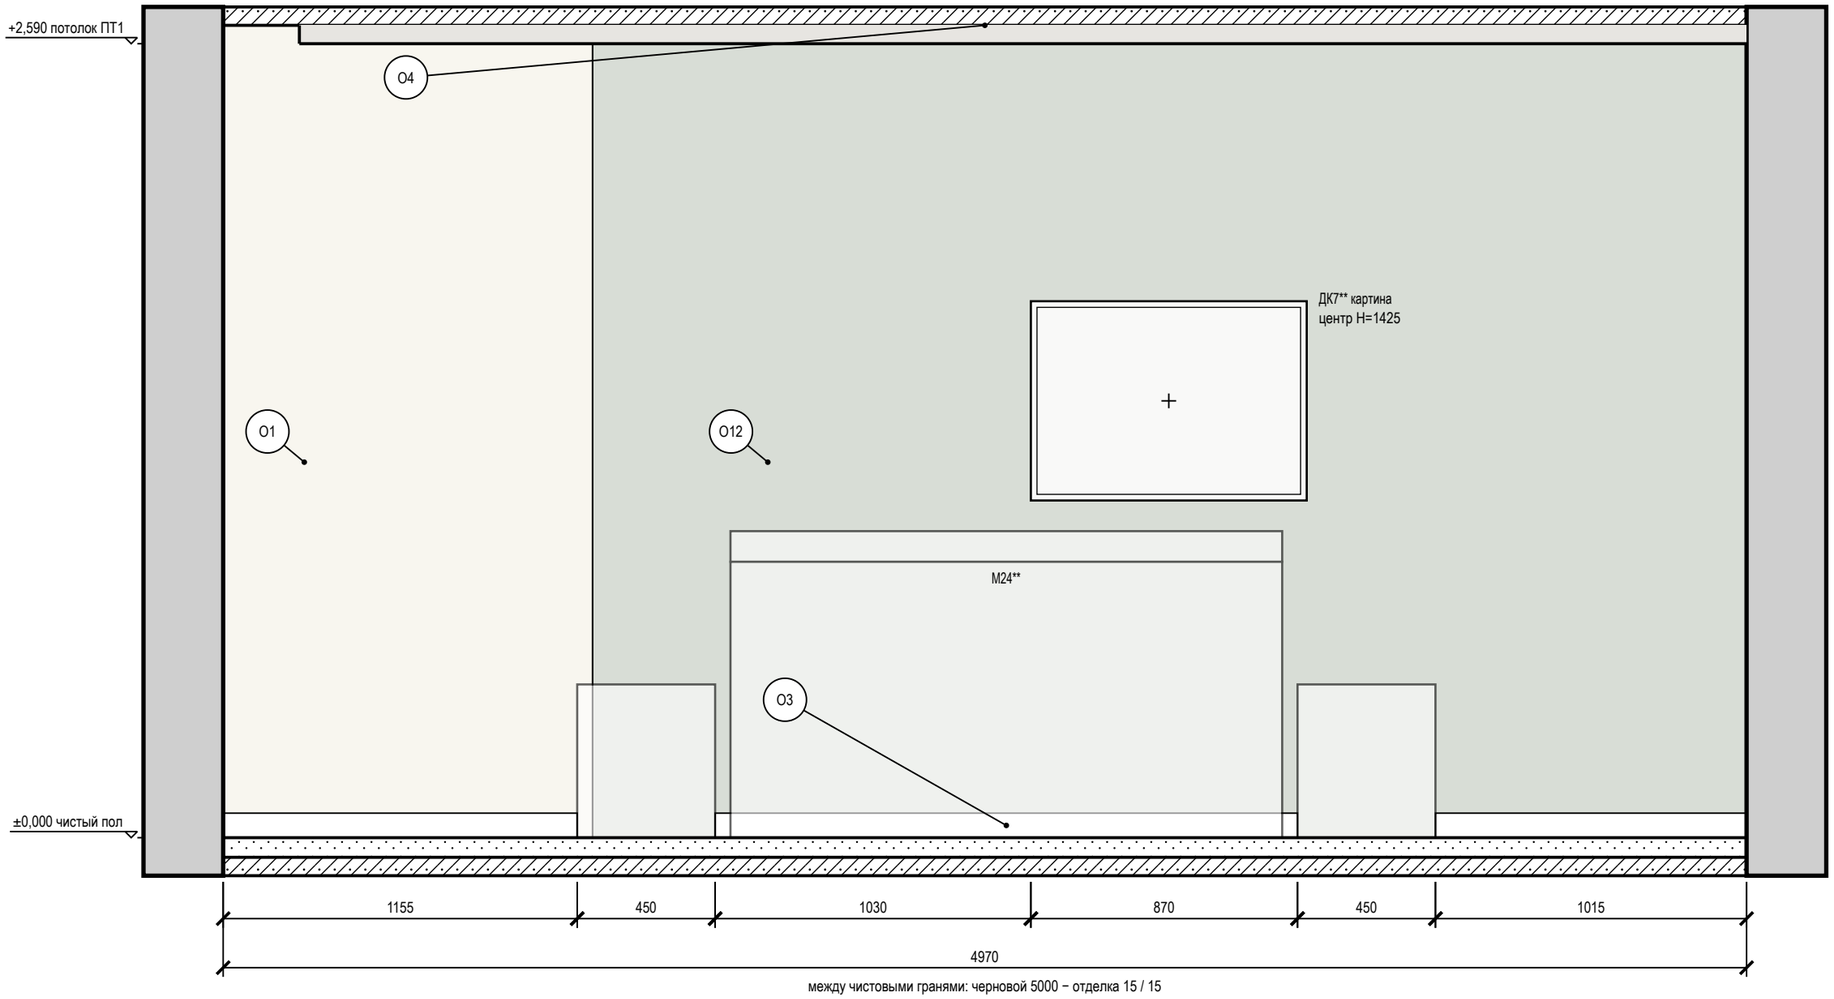

между чистовыми гранями: черновой 5000 − отделка 15 / 15

Схема развёрток (М 1:100)

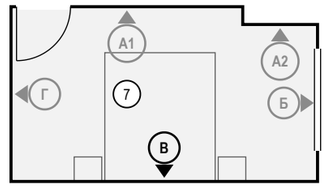

Допущения и предложения на листе

Основа листа: планировка по обводу плана заказчика, не замерена (К-1); высота до плиты 2650 мм от чистого пола — решение автора (ИЗ-1); отметки плана потолков сдвинуты на -95 мм (+2.745 плана = низ плиты), не замерено (К-2); толщины стен приняты: наружные 260 мм, перегородки 130 мм (К-1); положение стен и проёмов — по брифу без обмера и плана БТИ (К-1); разрешённая мощность 10 кВт принята, ТУ не переданы (К-6); вентканалы приняты, в брифе не заданы (К-5); тип дома, перекрытие и несущие стены не известны — документов нет (К-3); плита электрическая — принята, в брифе не указано (К-6); система заземления TN-C-S принята, ТУ не переданы (К-6); число жильцов 2 принято, в брифе не указано (К-9); подрайон климата не задан — принят не северный (жилые от 2,5 м) (К-26).

Знак «*» — принято, не замерено и не подтверждено (замерить на объекте): К-1: окно пом. 7 (стена Б) — окно: положение, ширина, высота и подоконник приняты по обводу плана заказчика, без обмера, не замерены; дверь пом. 7 (стена А) — проём принят по обводу плана заказчика, без обмера: положение и ширина сняты с плана, не замерены.

Знак «**» — предложение проектировщика, заказчиком не утверждено (согласовать с заказчиком): ИЗ-2, К-7: М24 — по исходному плану: прикроватные светильники 13-А / 13-Б в 2480 мм друг от друга у стены С — двуспальная кровать 1800 по центру между ними; К-7: ДК7.

См. лист открытых вопросов (лист 5, записи К-1, К-3, К-5–К-7, К-9; лист 6, запись К-26; лист 7, запись ИЗ-2).

Условные обозначения

- мебель и приборы — фасад по расстановке (условно)
- картина (декор): марка Д, крест — центр, Н — высота центра, мм
- стены и перекрытия в сечении
- окраска: тон — цвет по коду производителя (условно)
- О1 — марка отделки по реестру отделки альбома
- А — марка развёртки: буква стены, стрелка — взгляд

Примечания

1. Развёртки — вид на стену изнутри помещения, по часовой стрелке; расположение — на схеме листа и на листе 71; размеры — в мм по чистовым поверхностям; отметки — в м от ±0,000; высоты Н — от чистого пола помещения до оси изделия, у декора — до центра.
2. Стена В показана двумя видами: здесь — архитектурная развёртка (мебель, отделка, проёмы, высоты), электроточки и выводы ВК с привязками и таблицей — на листе 96 («Привязки»).
3. Схема мебели, приборов и декора не является технической документацией для производства мебели; габариты — по паспортам изделий.
4. Картины и зеркала крепить к основанию по паспорту изделия (закладные и анкеры — в перечне скрытых работ); крест — ось центра предмета.

1000 мм · печать 1:1

Изм.	Кол.уч	Лист	№ док.	Подп.	Дата
Разраб.		Кырлан А.С.			04.11.26
Пров.					
ГИП					
Н. контр.					
Утв.					

ГД-2026-020-АИ

Квартира 68 м², элитный модерн

Общая площадь 68,47* м² · * размеры приняты, не замерены (реестр — л. 5–7, К-1)

Дизайн-проект интерьера

Стадия	Лист	Листов
РП	95	105

Развёртка стены В. Спальня (пом. 7)

М 1:20

Кырлан Александр Сергеевич

Привязки электроточек, стена В. Спальня (пом. 7)

Спальня (пом. 7) · вид изнутри помещения · привязки в мм, отметки в м · к развёртке на листе 95

ПРЕДВАРИТЕЛЬНО · не для производства работ · открыто пунктов: 25 (реестр — л. 5–7)

Развёртка стены В: электроточки и выводы

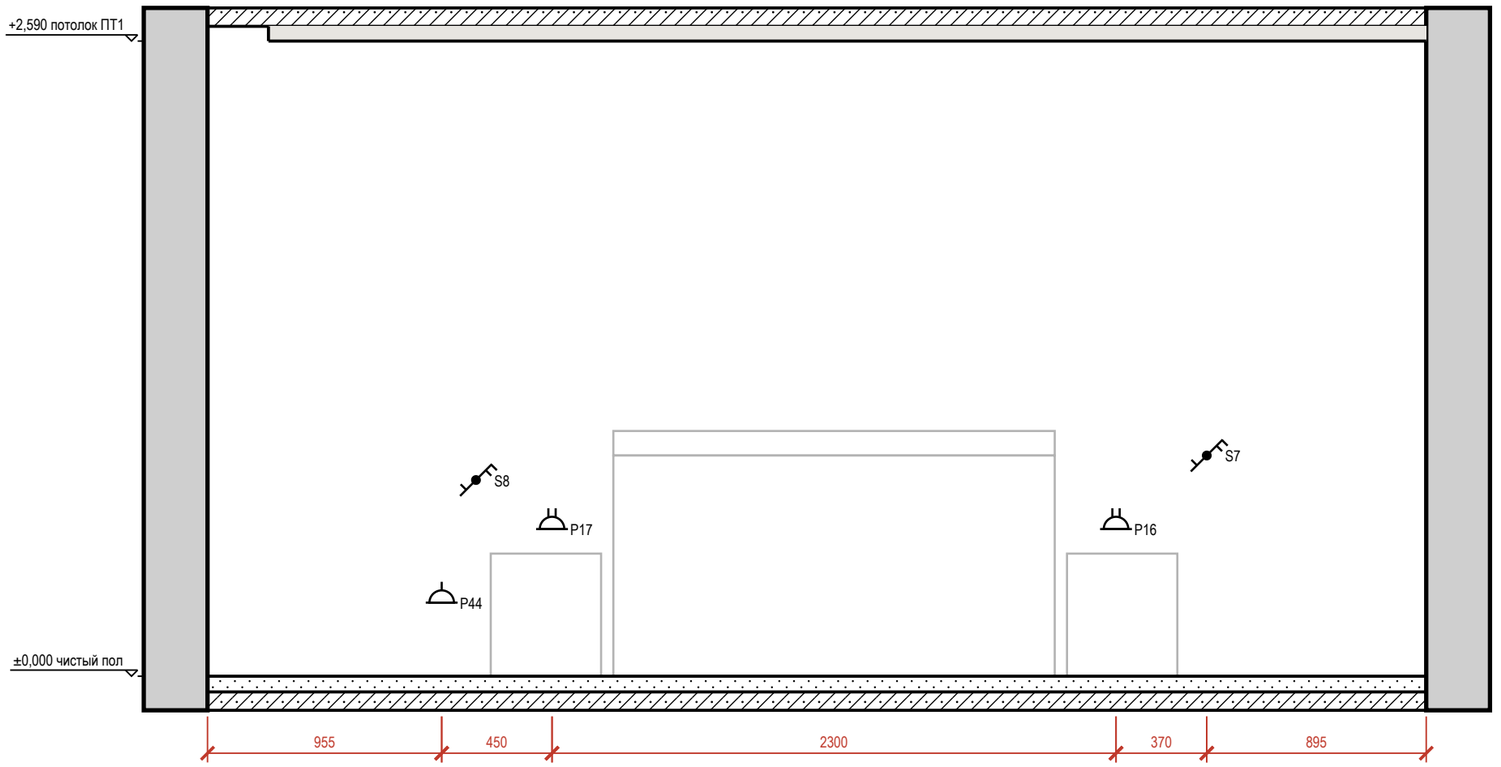



Таблица привязок электроточек и выводов

Марка	Назначение	От угла, мм	Н от пола, мм	Примечание
P44	розетка: общего назначения	955	300	гр. 6
S8	выключатель	1095	800	гр. 1
P17	розетка: у кровати: лампа, зарядка	1405	600	рамка 2 поста, гр. 6
P16	розетка: у кровати: лампа, зарядка	3705	600	рамка 2 поста, гр. 6
S7	выключатель	4075	900	гр. 1

Условные обозначения

- розетка с заземляющим контактом; у знака — марка, ×N постов в рамке, гр. — группа щита, Н — высота оси, мм
- выключатель одноклавишный
- выключатель двухклавишный (флажков — по числу клавиш)
- выключатель с проходной или перекрёстной клавишей (обратный флажок); тип клавиши — в подписи
- привязки точек и выводов от угла и от пола, мм
- марка развёртки: буква стены, стрелка — взгляд

Схема развёрток (М 1:50)

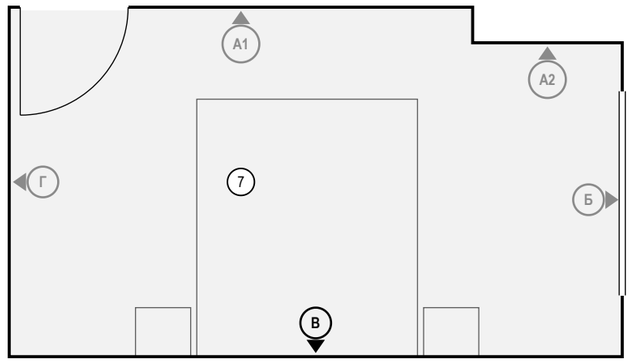

Примечания

1. Вид «Привязки» стены В — электроточки и выводы ВК; архитектурная развёртка (мебель, отделка, проёмы, высоты) — на листе 95, расположение — на листе 71. Мебель и приборы — подложкой для ориентира; их марки и обозначения мебели, проёмов и стен — там же.
2. Привязки — в мм: по горизонтали от левого чистового угла стены до оси изделия, Н — от чистого пола до оси; все точки — в таблице привязок. Красная цепочка — привязки по осям; точки ближе 150 мм одна к другой в цепочку не дробятся — их привязки только в таблице.
3. У знака — марка электроточки (Р — розетка, S — выключатель, Св — светильник, ЭВ — вывод кабеля); посты в рамке и группа щита — в графе «Примечание»; группы по клавишам выключателя — на листе выключателей.

Допущения и предложения на листе

Основа листа: планировка по обводу плана заказчика, не замерена (К-1); высота до плиты 2650 мм от чистого пола — решение автора (ИЗ-1); отметки плана потолков сдвинуты на -95 мм (+2.745 плана = низ плиты), не замерено (К-2); толщины стен приняты: наружные 260 мм, перегородки 130 мм (К-1); положение стен и проёмов — по брифу без обмера и плана БТИ (К-1); разрешённая мощность 10 кВт принята, ТУ не переданы (К-6); вентканалы приняты, в брифе не заданы (К-5); тип дома, перекрытие и несущие стены не известны — документов нет (К-3); плита электрическая — принята, в брифе не указано (К-6); система заземления TN-C-S принята, ТУ не переданы (К-6); число жильцов 2 принято, в брифе не указано (К-9); подрайон климата не задан — принят не северный (жилые от 2,5 м) (К-26).

Знак «*» — принято, не замерено и не подтверждено (замерить на объекте): К-1: окно пом. 7 (стена Б) — окно: положение, ширина, высота и подоконник приняты по обводу плана заказчика, без обмера, не замерены; дверь пом. 7 (стена А) — проём принят по обводу плана заказчика, без обмера: положение и ширина сняты с плана, не замерены.

См. лист открытых вопросов (лист 5, записи К-1, К-3, К-5, К-6, К-9; лист 6, запись К-26).

1000 мм · печать 1:1

Изм.	Кол.уч	Лист	№ док.	Подп.	Дата
Разраб.		Кырлан А.С.			04.11.26
Пров.					
ГИП					
Н. контр.					
Утв.					

ГД-2026-020-АИ

Квартира 68 м², элитный модерн

Общая площадь 68,47* м² · * размеры приняты, не замерены (реестр — л. 5–7, К-1)

Дизайн-проект интерьера	Стадия	Лист	Листов
	РП	96	105

Привязки электроточек, стена В. Спальня (пом. 7)

М 1:25

Кырлан Александр Сергеевич


выпуск 04.11.2026 № 8be4ef4c81 · стр. 105 из 117

Развёртка стены Г. Спальня (пом. 7)

Спальня (пом. 7) · вид изнутри помещения · размеры в мм, отметки в м


ПРЕДВАРИТЕЛЬНО · не для производства работ · открыто пунктов: 25 (реестр — л. 5–7)

Развёртка стены Г

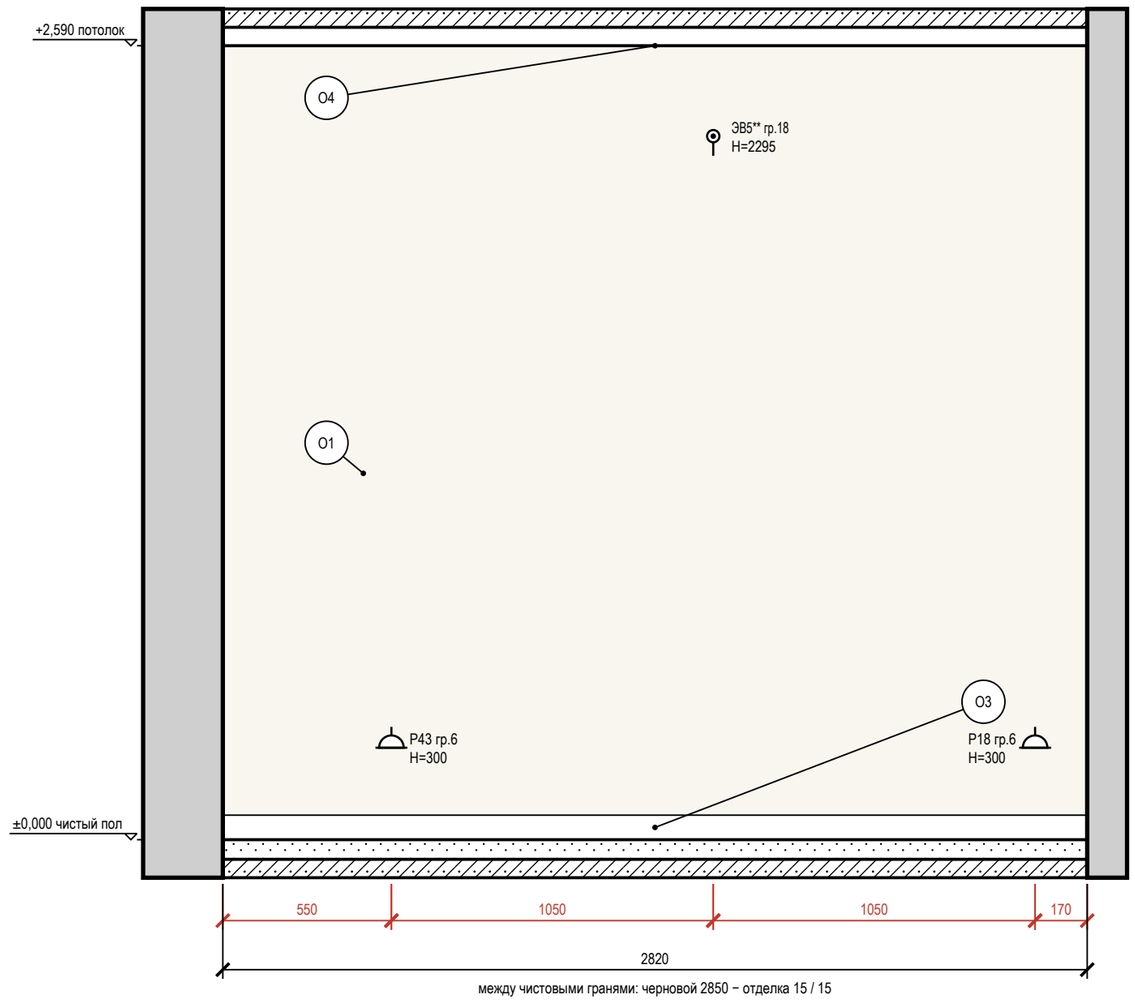

между чистовыми гранями: черновой 2850 − отделка 15 / 15

Схема развёрток (М 1:100)

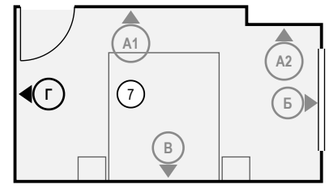

Условные обозначения

- розетка с заземляющим контактом; у знака — марка, ×N постов в рамке, гр. — группа щита, Н — высота оси, мм
- вывод кабеля для подключения прибора (без розетки), марка ЭВ
- привязки точек и выводов от угла и от пола, мм
- мебель и приборы — фасад по расстановке (условно)
- стены и перекрытия в сечении
- окраска: тон — цвет по коду производителя (условно)
- О1 — марка отделки по реестру отделки альбома
- А — марка развёртки: буква стены, стрелка — взгляд

Ведомость отделки (на листе)

Марка	Поверхность	Материал, изделие	Цвет, код	Кол.
О1	стены	окраска, Farrow & Ball Modern Emulsion, матовая, подготовка Q3	Farrow & Ball No. 2003 «Pointing»	7,3 м²
О3	плинтус	плинтус МДФ, h 80 мм, аналог: плинтус МДФ под покраску 80×16	Farrow & Ball No. 2003 «Pointing»	2,8 м
О4	потолок	окраска, Tikkurila Euro Power 7, глубокоматовая, подготовка Q3	Tikkurila G503 «Calla»	13,9 м²

Допущения и предложения на листе

Основа листа: планировка по обводу плана заказчика, не замерена (К-1); высота до плиты 2650 мм от чистого пола — решение автора (ИЗ-1); отметки плана потолков сдвинуты на -95 мм (+2.745 плана = низ плиты), не замерено (К-2); толщины стен приняты: наружные 260 мм, перегородки 130 мм (К-1); положение стен и проёмов — по брифу без обмера и плана БТИ (К-1); разрешённая мощность 10 кВт принята, ТУ не переданы (К-6); вентканалы приняты, в брифе не заданы (К-5); тип дома, перекрытие и несущие стены не известны — документов нет (К-3); плита электрическая — принята, в брифе не указано (К-6); система заземления TN-C-S принята, ТУ не переданы (К-6); число жильцов 2 принято, в брифе не указано (К-9); подрайон климата не задан — принят не северный (жилые от 2,5 м) (К-26).

Знак «*» — принято, не замерено и не подтверждено (замерить на объекте): К-1: окно пом. 7 (стена Б) — окно: положение, ширина, высота и подоконник приняты по обводу плана заказчика, без обмера, не замерены; дверь пом. 7 (стена А) — проём принят по обводу плана заказчика, без обмера: положение и ширина сняты с плана, не замерены.

Знак «**» — предложение проектировщика, заказчиком не утверждено (согласовать с заказчиком): ЭВ5 — питание внутреннего блока КВ-2: отдельная линия С16, вывод рядом с блоком под потолком.

См. лист открытых вопросов (лист 5, записи К-1, К-3, К-5, К-6, К-9; лист 6, запись К-26).

Примечания

1. Развёртки — вид на стену изнутри помещения, по часовой стрелке; расположение — на схеме листа и на листе 71; размеры — в мм по чистовым поверхностям; отметки — в м от ±0,000; высоты Н — от чистого пола помещения до оси изделия, у декора — до центра.
2. Красная цепочка — привязки электроточек и выводов по осям от угла чистовых стен; высота Н — у знака, от чистого пола до оси; высоты мебели, проёмов и границ отделки — колонкой отметок слева. Стена с 5 и более точками или с мелкими звеньями привязок показана двумя видами: архитектурная развёртка (мебель, отделка, проёмы, высоты) и вид «Привязки» на отдельном листе — точки и выводы с марками, одна цепочка по осям и таблица привязок (каждая точка — строка).
3. У знака электроточки: марка (Р — розетка, S — выключатель, Св — светильник, ЭВ — вывод кабеля), ×N — число постов в рамке, гр. — группа щита, Н — высота оси от чистого пола, мм; группы по клавишам выключателя — на листе выключателей.
4. Схема мебели, приборов и декора не является технической документацией для производства мебели; габариты — по паспортам изделий.

1000 мм · печать 1:1

Изм.	Кол.уч	Лист	№ док.	Подп.	Дата
Разраб.		Кырлан А.С.			04.11.26
Пров.					
ГИП					
Н. контр.					
Утв.					

ГД-2026-020-АИ

Квартира 68 м², элитный модерн

Общая площадь 68,47* м² · * размеры приняты, не замерены (реестр — л. 5–7, К-1)

Дизайн-проект интерьера

Стадия	Лист	Листов
РП	97	105

Развёртка стены Г. Спальня (пом. 7)

М 1:20

Кырлан Александр Сергеевич


выпуск 04.11.2026 № 8be4ef4c81 · стр. 106 из 117

Узлы

Пороги и стыки покрытий, скрытые двери, короба стояков, гидроизоляция, плинтус


1 Порог 15 мм: мокрая зона — смежное помещение (М 1:5)

Применение: двери Д-2, Д-3; места — лист 71

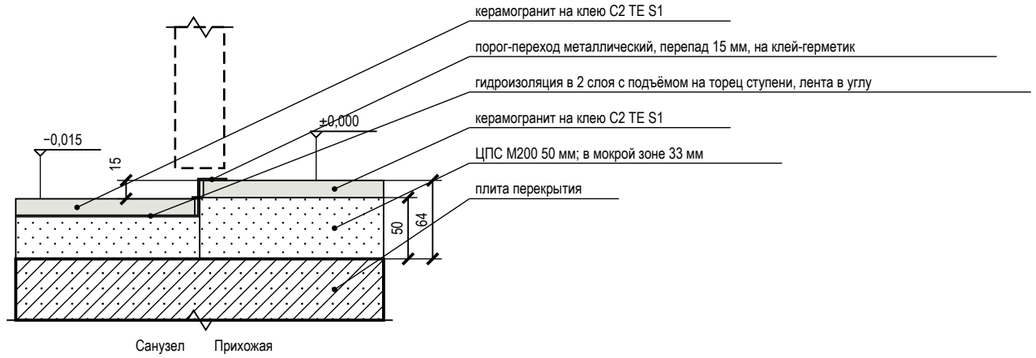


2 Короб стояков К1-1 с люком и звукоизоляцией (М 1:20)

Применение: пом. 3; места — лист 71

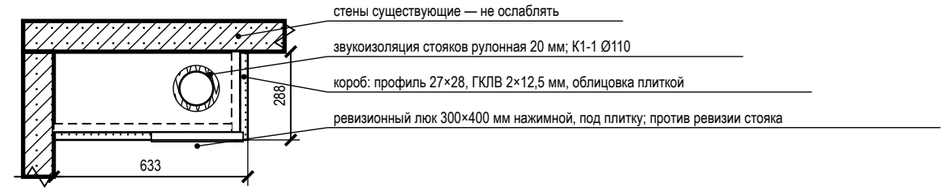


3 Гидроизоляция санузла: заход на стены 200 мм, примыкание ванны (М 1:20)

Применение: пом. 2, 3; места — лист 71

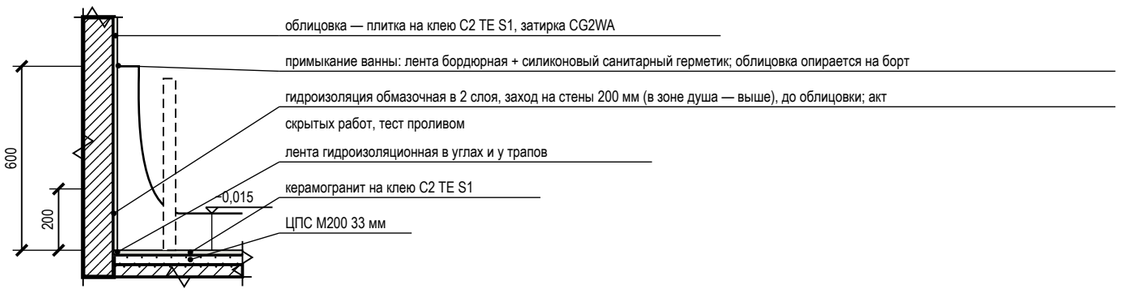


4 Плинтус МДФ 80×16 мм у окрашенной стены по доске (ламинату) (М 1:10)

Применение: пом. 1, 5, 6, 7; места — лист 71

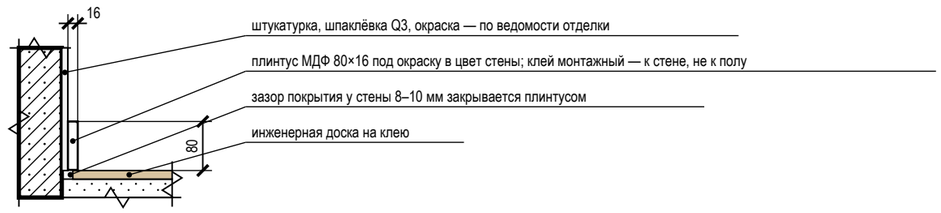

5 Плинтус МДФ 80×16 мм у окрашенной стены по керамограниту (плитке) (М 1:10)

Применение: пом. 4; места — лист 71

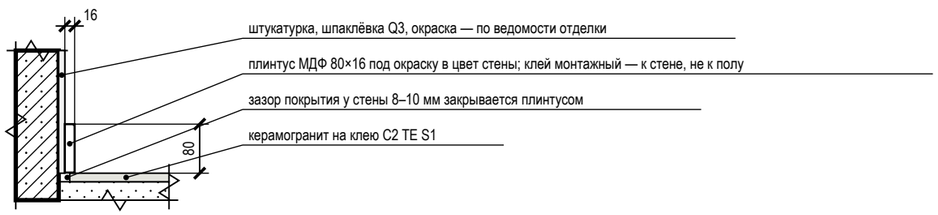

Допущения и предложения на листе

Основа листа: планировка по обводу плана заказчика, не замерена (К-1); высота до плиты 2650 мм от чистого пола — решение автора (ИЗ-1); отметки плана потолков сдвинуты на -95 мм (+2.745 плана = низ плиты), не замерено (К-2); толщины стен приняты: наружные 260 мм, перегородки 130 мм (К-1); положение стен и проёмов — по брифу без обмера и плана БТИ (К-1); разрешённая мощность 10 кВт принята, ТУ не переданы (К-6); вентканалы приняты, в брифе не заданы (К-5); тип дома, перекрытие и несущие стены не известны — документов нет (К-3); плита электрическая — принята, в брифе не указано (К-6); система заземления TN-C-S принята, ТУ не переданы (К-6); число жильцов 2 принято, в брифе не указано (К-9); подрайон климата не задан — принят не северный (жилые от 2,5 м) (К-26).

См. лист открытых вопросов (лист 5, записи К-1, К-3, К-5, К-6, К-9; лист 6, запись К-26).

Условные обозначения

- железобетон (плита, стены) — условно: конструкция не установлена
- кладка, перегородка — условно: конструкция не установлена
- стяжка, раствор
- гипсокартон ГКЛВ
- звукоизоляция, эластичный заполнитель
- плитка, керамогранит на клею
- инженерная доска (покрытие пола)
- металлический профиль (порог, Т-профиль, короб двери)
- гидроизоляция (обмазочная, лента)

Примечания

1. Узлы — типовые решения проекта для мест, отмеченных выносками на листе схемы расположения развёрток и узлов; размеры — в мм, отметки — в м от ±0,000.
2. Узлы с гидроизоляцией, закладными и коробами скрытого монтажа принимаются по актам скрытых работ до закрытия отделкой; гидроизоляция — после теста проливом (24 ч).
3. Марки изделий (порог, Т-профиль, короб скрытой двери, люк) — по спецификациям; замена — на аналог с теми же габаритами по согласованию с автором проекта.
4. Материал плиты перекрытия и стен в узлах показан условно (железобетон, кладка): конструкция дома не установлена — крепёж, анкеры и толщины слоёв уточняются после обследования (до него — по допущениям общих указаний).

Изм.	Кол.уч	Лист	№ док.	Подп.	Дата
Разраб.		Кырлан А.С.			04.11.26
Пров.					
ГИП					
Н. контр.					
Утв.					

ГД-2026-020-АИ

Квартира 68 м², элитный модерн

Общая площадь 68,47* м² · * размеры приняты, не замерены (реестр — л. 5–7, К-1)

Дизайн-проект интерьера	Стадия	Лист	Листов
	РП	98	105

Узлы

М 1:5; 1:20; 1:10

Кырлан Александр Сергеевич

выпуск 04.11.2026 № 8be4ef4c81 · стр. 107 из 117

10

Смета

Кырлан Александр Сергеевич

выпуск 04.11.2026 · 8be4ef4c81 · стр. 108 из 117

Ведомость объёмов работ

ПРЕДВАРИТЕЛЬНО · не для производства работ · открыто пунктов: 25 (реестр — л. 5–7)

Объёмы по помещениям от чертежа · площади в м², длины в м · формула, правило проёмов и источник в каждой строке

Ведомость объёмов работ по помещениям

Поз.	Наименование работ (материал, число слоёв)	Ед. изм.	Объём по помещениям (№ по экспликации)							Всего	Формула подсчёта	Правило проёмов	Источник	Цена за ед., ₽	Стоимость, ₽
			1	2	3	4	5	6	7						
1. Демонтаж и черновые работы															
1	Демонтаж существующего покрытия пола до основания	м²	10,61	1,85	3,96	13,87	12,04	12,24	13,90	68,47	S пом.		л. 15, 16	по КП	
2	Демонтаж существующей отделки стен до основания	м²	29,72	12,40	18,65	27,58	34,20	32,28	36,32	191,15	P × H − проёмы	за вычетом проёмов	л. 15, 16	по КП	
3	Демонтаж существующей отделки потолка до основания	м²	10,61	1,85	3,96	13,87	12,04	12,24	13,90	68,47	S пом.		л. 15, 16	по КП	
4	Демонтаж существующих дверных блоков	шт	1	1	1	1	1	1	1	7	по ведомости проёмов		л. 16, 17	по КП	
5	Демонтаж существующих сантехприборов и электрооборудования (если есть)	компл									по факту на объекте		л. 16	по КП	
6	Устройство стяжки: стяжка ЦПС М200, 50 мм	м²	10,67	1,90	4,01	14,32	12,10	12,30	13,96	69,26	S пом. + S в дверных проёмах (b × t/2)	проёмы добавлены	л. 53–55	530	36 708
7	Гидроизоляция обмазочная, 2 слоя: пол, стены на 200 мм, зоны замачивания	м²		2,64	11,68					14,32	пол + (P − двери) × h заведения + зоны замачивания		л. 49	450	6 444
8	Штукатурка стен по маякам, до 10 мм	м²	29,72	12,40	18,65	27,58	34,20	32,28	36,32	191,15	P × H − проёмы по обводу коробок − грани перегородок на ГКЛВ	за вычетом проёмов	л. 15, 54, 55	530	101 310
9	Штукатурка оконных откосов шириной до 200 мм	м²	0,88				0,82	0,89	0,89	3,48	Σ (2h + b) × глубина откоса	откосы ≤ 200 мм	л. 15	540	1 879
10	Потолок ГКЛ по каркасу П113, 1 слой	м²	10,61	1,85	3,96	13,44	12,04	12,24	13,90	68,04	S пом. по плану потолков		л. 45–48	1 500	102 060
Итого по разделу 1 — 248 401 ₽ (позиций 10, из них по КП 5); в сводную смету — л. 104, 105															
2. Инженерные системы															
11	Прокладка кабеля ВВГнг(A)-LS по группам щита: за потолком и в штробах стен (штробы только после технического заключения, см. строку «Штробы в стенах»)	м								571,00	Σ длин групп щита		л. 28, 29	60	34 260
12	Прокладка слаботочной линии: Кабель домофона — тип по системе поставщика, отдельно от силовых	м								3,10	по лучам от ЩС**: 1 точ., запас 10 %		л. 31	по КП	
13	Прокладка слаботочной линии: Кабель коаксиальный RG-6 (75 Ом) к розеткам ТВ, отдельно от силовых	м								14,10	по лучам от ЩС**: 1 точ., запас 10 %		л. 31	по КП	
14	Прокладка слаботочной линии: Кабель U/UTP кат. 5e (LAN, Wi-Fi и камеры по PoE), отдельно от силовых	м								27,40	по лучам от ЩС**: 2 точ., запас 10 %		л. 31	по КП	
15	Прокладка слаботочной линии: Кабель U/UTP кат. 6 (LAN, Wi-Fi и камеры по PoE), отдельно от силовых	м								2,70	по лучам от ЩС**: 1 точ., запас 10 %		л. 31	по КП	
16	Прокладка гофротрубы Ø20 для слаботочных линий, отдельно от силовых	м								42,60	по длине лучей без участков в канале плинтуса (≈ 90 %)		л. 31	по КП	
17	Сборка слаботочного щита ЩС**: корпус, патч-панель, подключение линий и питания 220 В; коммутатор и точки доступа — оборудование заказчика	шт								1	один щит		л. 26, 27, 31	по КП	
18	Электроточка: подрозетник в бетоне, розетка, выключатель, вывод	шт	11	2	3	12	15	15	15	73	по ведомости электроточек		л. 23, 26, 27	950	69 350
19	Штробы в стенах под спуски кабеля к точкам — выполняются только после технического заключения о несущих стенах	м	19,44	1,54	2,96	19,15	23,80	24,40	27,90	119,19	Σ (H − h) по точкам на стенах: вертикальные спуски	после техзаключения	л. 16, 23	по КП	
20	Установка встраиваемого точечного светильника	шт	6	1	6	9	6	6	8	42	по плану освещения		л. 24	750	31 500
21	Монтаж светильника: потолочного, подвесного, настенного	шт	1						2	3	по плану освещения		л. 24	1 200	3 600
22	Монтаж LED-ленты в алюминиевый профиль	м					3,00			3,00	Σ длин лент по плану освещения		л. 24	230	690
23	Установка блока питания LED в доступном месте (люк, шкаф)	шт					1			1	один на LED-группу		л. 24	570	570

Допущения и предложения на листе

Основа листа: планировка по обводу плана заказчика, не замерена (К-1); высота до плиты 2650 мм от чистого пола — решение автора (ИЗ-1); отметки плана потолков сдвинуты на -95 мм (+2.745 плана = низ плиты), не замерено (К-2); толщины стен приняты: наружные 260 мм, перегородки 130 мм (К-1); положение стен и проёмов — по брифу без обмера и плана БТИ (К-1); разрешённая мощность 10 кВт принята, ТУ не переданы (К-6); вентканалы приняты, в брифе не заданы (К-5); тип дома, перекрытие и несущие стены не известны — документов нет (К-3); плита электрическая — принята, в брифе не указано (К-6); система заземления TN-C-S принята, ТУ не переданы (К-6); число жильцов 2 принято, в брифе не указано (К-9); подрайон климата не задан — принят не северный (жилые от 2,5 м) (К-26).

Знак «**» — предложение проектировщика, заказчиком не утверждено (согласовать с заказчиком): ЩС — щит слаботочный: место и состав.

См. лист открытых вопросов (лист 5, записи К-1, К-3, К-5, К-6, К-9; лист 6, запись К-26).

Изм.	Кол.уч	Лист	№ док.	Подп.	Дата
Разраб.		Кырлан А.С.			04.11.26
Пров.					
ГИП					
Н. контр.					
Утв.					

ГД-2026-020-АИ

Квартира 68 м², элитный модерн

Общая площадь 68,47* м² · * размеры приняты, не замерены (реестр — л. 5–7, К-1)

Дизайн-проект интерьера

Стадия	Лист	Листов
РП	99	105

Ведомость объёмов работ

М б/м

Кырлан Александр Сергеевич

Ведомость объёмов работ (продолжение)

ПРЕДВАРИТЕЛЬНО · не для производства работ · открыто пунктов: 25 (реестр — л. 5–7)

Объёмы по помещениям от чертежа · площади в м², длины в м · формула, правило проёмов и источник в каждой строке

Ведомость объёмов работ по помещениям (продолжение)

Поз.	Наименование работ (материал, число слоёв)	Ед. изм.	Объём по помещениям (№ по экспликации)							Всего	Формула подсчёта	Правило проёмов	Источник	Цена за ед., ₽	Стоимость, ₽
			1	2	3	4	5	6	7						
24	Установка автономного пожарного извещателя	шт	1			1	1	1	1	5	по плану розеток		л. 23	по КП	
25	Сборка щита: установка автоматов и АВДТ групп, вводного автомата	шт								21	группы + вводной автомат		л. 28, 29	230	4 830
26	Установка вводного УЗО	шт								1	по однолинейной схеме		л. 28, 29	380	380
27	Монтаж инсталляции, установка подвесного унитаза и кнопки смыва	шт		1						1	по плану выводов		л. 34, 43	10 500	10 500
28	Короб инсталляции: каркас и обшивка ГКЛВ в 2 слоя, ревизионный доступ к смыву	шт		1	1					2	по плану выводов		л. 34, 49–52	по КП	
29	Короб К1 над чистым полом: каркас и обшивка ГКЛВ под плитку (материалы — в спецификации ВК)	м.п.		0,89	1,18					2,07	Σ открытых участков выпусков К1 (профиль листа разводки ВК)		л. 34, 43	по КП	
30	Установка ванны с сифоном	шт			1					1	по плану выводов		л. 34, 43	6 000	6 000
31	Установка умывальника (мойки) с сифоном и смесителем	шт		1	1		1			3	по плану выводов		л. 34, 43	3 000	9 000
32	Подключение стиральной (посудомоечной) машины к ВК	шт			1		1			2	по плану выводов		л. 34	по КП	
33	Установка радиатора с узлом подключения и терморегулятором	шт	1				1	1	1	4	по плану отопления		л. 33	по КП	
34	Электрический тёплый пол: укладка нагревательного мата в слой клея, датчик пола в гофротрубе	м²			1,06	1,94				3,00	Σ контуров по плану ЭОМ (полезная площадь)		л. 23, 53	750	2 250
35	Установка терморегулятора тёплого пола с датчиком в гофротрубе	шт			1	1				2	один на контур		л. 23	750	1 500
Итого по разделу 2 — 174 430 ₽ (позиций 25, из них по КП 12); в сводную смету — л. 104, 105															
3. Чистовые работы															
36	Облицовка стен керамогранитом 600×1200 на клею	м²		11,04	17,72					28,76	по раскладке: зона облицовки − место за коробом	за вычетом проёмов	л. 49–52	2 500	71 900
37	Облицовка короба инсталляции (ГКЛВ) керамогранитом: лицо, боковины, полка	м²		1,47						1,47	по раскладке: лицо, боковины, полка		л. 49–52	2 500	3 675
38	Облицовка фартука керамогранитом 1200×600	м²					1,68			1,68	по раскладке фартука		л. 49–52, 54, 55	2 400	4 032
39	Укладка керамогранита на пол, 600×600, на клею	м²		1,90	4,01	14,32				20,23	S пом. + S в дверных проёмах	проёмы добавлены	л. 49–53	1 800	36 414
40	Затирка швов керамогранита	м²		14,36	21,68	13,87	1,68			51,59	Σ S облицовки и пола из плитки		л. 49–52	150	7 739
41	Грунтование стен, 2 слоя (под штукатурку и под отделку)	м²	29,72	12,40	18,65	27,58	34,20	32,28	36,32	191,15	P × H − проёмы	за вычетом проёмов	л. 54, 55	96	18 350
42	Шпаклёвка стен под окраску, 2 слоя (старт и финиш), уровень Q3	м²	29,72			27,58	32,52	32,28	36,32	158,42	P × H − проёмы − фартук	за вычетом проёмов	л. 54, 55	750	118 815
43	Грунтование и шпаклёвка оконных откосов, 2 слоя	м.п.	4,64				4,30	4,67	4,67	18,28	Σ (2h + b) по окнам	по окнам	л. 15	300	5 484
44	Грунтование потолка, 2 слоя	м²	10,61	1,85	3,96	13,87	12,04	12,24	13,90	68,47	S пом.		л. 54, 55	96	6 573
45	Шпаклёвка потолка под окраску, 2 слоя, уровень Q3	м²	10,61	1,85	3,96	13,87	12,04	12,24	13,90	68,47	S пом.		л. 45–48, 54, 55	950	65 047
46	Окраска потолка водно-дисперсионной краской, 2 слоя	м²	10,61	1,85	3,96	13,87	12,04	12,24	13,90	68,47	S пом.		л. 54, 55	360	24 649
47	Окраска стен водно-дисперсионной краской, 2 слоя	м²	34,03			40,14	36,32	36,62	40,66	187,77	P × H − фартук, проёмы не вычитаются	без вычета проёмов	л. 54, 55	300	56 331
48	Окраска оконных откосов, 2 слоя	м.п.	4,64				4,30	4,67	4,67	18,28	Σ (2h + b) по окнам	по окнам	л. 15	120	2 194
49	Укладка инженерной доски на клей	м²	10,67				12,10	12,30	13,96	49,03	S пом. + S в дверных проёмах	проёмы добавлены	л. 53–55	1 200	58 836
50	Установка плинтуса МДФ h=80 мм	м.п.	12,26			9,76	13,79	13,26	14,82	63,89	P − ширина дверных проёмов		л. 54, 55	450	28 751

Допущения и предложения на листе

Основа листа: планировка по обводу плана заказчика, не замерена (К-1); высота до плиты 2650 мм от чистого пола — решение автора (ИЗ-1); отметки плана потолков сдвинуты на -95 мм (+2.745 плана = низ плиты), не замерено (К-2); толщины стен приняты: наружные 260 мм, перегородки 130 мм (К-1); положение стен и проёмов — по брифу без обмера и плана БТИ (К-1); разрешённая мощность 10 кВт принята, ТУ не переданы (К-6); вентканалы приняты, в брифе не заданы (К-5); тип дома, перекрытие и несущие стены не известны — документов нет (К-3); плита электрическая — принята, в брифе не указано (К-6); система заземления TN-C-S принята, ТУ не переданы (К-6); число жильцов 2 принято, в брифе не указано (К-9); подрайон климата не задан — принят не северный (жилые от 2,5 м) (К-26).

См. лист открытых вопросов (лист 5, записи К-1, К-3, К-5, К-6, К-9; лист 6, запись К-26).

Изм.	Кол.уч	Лист	№ док.	Подп.	Дата
Разраб.		Кырлан А.С.			04.11.26
Пров.					
ГИП					
Н. контр.					
Утв.					

ГД-2026-020-АИ

Квартира 68 м², элитный модерн

Общая площадь 68,47* м² · * размеры приняты, не замерены (реестр — л. 5–7, К-1)

Дизайн-проект интерьера

Стадия	Лист	Листов
РП	100	105

Ведомость объёмов работ (продолжение)

М б/м

Кырлан Александр Сергеевич

Ведомость объёмов работ (окончание)

Объёмы по помещениям от чертежа · площади в м², длины в м · формула, правило проёмов и источник в каждой строке

Ведомость объёмов работ по помещениям (продолжение)

Поз.	Наименование работ (материал, число слоёв)	Ед. изм.	Объём по помещениям (№ по экспликации)							Всего	Формула подсчёта	Правило проёмов	Источник	Цена за ед., ₽	Стоимость, ₽
			1	2	3	4	5	6	7						
51	Окраска плинтуса в тоне No. 2003, 2 слоя	м.п.	12,26			9,76	13,79	13,26	14,82	63,89	как плинтус		л. 54, 55	300	19 167
52	Монтаж межкомнатных дверей (поставщик дверей)	шт	1	1	1		1	1	1	6	по ведомости проёмов		л. 17	5 250	31 500
53	Входная дверь, поставка с монтажом и откосами	шт								1	по ведомости проёмов		л. 17	по КП	
Итого по разделу 3 — 559 457 ₽ (позиций 18, из них по КП 1); в сводную смету — л. 104, 105															

Ведомость подсчёта площадей по помещениям

№	Помещение	S пола, м²	P, м	H, м	P × H, м²	Проёмы, м²	Стены нетто, м²	В дверных проёмах, м²	Плинтус, м	Откосы, м.п.
1	Кабинет	10,61	13,14	2,59	34,03	4,31	29,72	0,06	12,26	4,64
2	Санузел	1,85	5,58	2,52	14,06	1,66	12,40	0,05	нет	нет
3	Ванная	3,96	8,06	2,52	20,31	1,66	18,65	0,05	нет	нет
4	Прихожая	13,87	15,74	2,55	40,14	12,56	27,58	0,45	9,76	нет
5	Кухня-столовая	12,04	14,67	2,59	38,00	3,80	34,20	0,06	13,79	4,30
6	Гостиная	12,24	14,14	2,59	36,62	4,35	32,28	0,06	13,26	4,67
7	Спальня	13,90	15,70	2,59	40,66	4,35	36,32	0,06	14,82	4,67
	Итого	**68,47**			**223,82**	**32,67**	**191,15**	**0,78**	**63,89**	**18,27**

Реестр контрольных сумм

Показатель	По ВОР	По чертежу	Расхождение	Лист
Σ площадей помещений без летних, м² — общая площадь по экспликации	68,47	68,47	0,0 %	л. 15
Стены под окраску, м² (шпаклёвка) ведомость отделки	158,42	158,41	0,0 %	л. 54, 55
Потолки под окраску, м² — ведомость отделки	68,47	68,47	0,0 %	л. 54, 55
Плинтус, м — ведомость отделки	63,89	63,89	0,0 %	л. 54, 55
Плитка к заказу, шт — ведомость плитки	115	115	0,0 %	л. 49
Гидроизоляция, м² — ведомость материалов плитки	14,32	14,32	0,0 %	л. 49
Точки ЭОМ, шт — планы ЭОМ (без щитов)	125	128	-2,3 %	л. 23, 24

Примечания

1. Объёмы — от геометрии проекта (та же, что на планах и в ведомости отделки), не от общей площади: P — периметр чистого контура, H — от чистого пола до низа потолка, проёмы — по наружному обводу коробок.
2. Подсчёт по ГЭСН-2001-15 и ГЭСН-2001-11: штукатурка и шпаклёвка стен — за вычетом проёмов; окраска водными составами — без вычета проёмов (п. 2.24); откосы — отдельно, по ширине до 200 и более 200 мм; полы — с площадью в дверных проёмах.
3. Плитка — по раскладке (целые и с подрезкой); короб инсталляции и фартук — отдельными строками, двойного счёта облицовки нет. Материалы, запас и количество к заказу — в спецификации материалов.
4. Цены — ориентир по открытым прайсам Москвы (прайсы собраны 21.09.2026, часть расценок сверена повторно 24.09.2026), не коммерческое предложение; «по КП» — расценки нет, строка в итог не входит.
5. Демонтаж — по плану демонтажа и общим указаниям: покрытия пола, отделка стен и потолков, дверные блоки — до основания; объёмы справочные — по плану демонтажа (расценки в книге нет — «по КП»).
6. Штробы в стенах — только после технического заключения о несущих стенах (общие указания, план обмера и демонтажа): строка «Штробы в стенах» вертикальные спуски кабеля от потолочной трассы к точкам, объём не меньше фактического (горизонтальные трассы — по исполнительной схеме). Расценки штробления в прайсе нет — «по КП», в итог не входит; кабель в штробах стен прокладывается после неё.
7. Площадь облицовки стен — одно число с тремя названиями: зона облицовки по ведомости отделки 29,48 м² − место за коробом инсталляции 0,72 м² (плитку туда не кладут) = стены под плитку 28,76 м² (строка «Облицовка стен»); облицовка коробов 1,47 м² — отдельной строкой; стены и короба вместе — 30,23 м² (столько плитки по раскладке в спецификации). Источник — один (quantities.js), расхождение на листах ловит.
8. Слаботочные сети: кабель по лучам от ЩС** 47,30 м (U/UTP, RG-6, домофон — по видам), гофра 42,60 м, щит ЩС** с патч-панелью; розетки RJ45 и ТВ монтируются в строке «Электроточка». Длины те же, что в ведомости изделий электрика (одна модель — lowcurrent-engineer/bom.js); оборудование заказчика (точки доступа, камеры, коммутатор) в спецификацию не входит. 1 точ. — предложение листа слаботочки.
9. Коробы: стояков (нет) и К1 над чистым полом (2,07 м открытых участков; труба К1 вдоль стен 18,64 м в короб не зашивается — она за приборами, в раме инсталляции и в шахтах). В спецификации ВК короб К1 заказывается с запасом 10 % — 2,30 м. Материалы коробов стояков и инсталляции — в спецификации материалов, К1 — в спецификации ВК.

Допущения и предложения на листе

Основа листа: планировка по обводу плана заказчика, не замерена (К-1); высота до плиты 2650 мм от чистого пола — решение автора (ИЗ-1); отметки плана потолков сдвинуты на -95 мм (+2.745 плана = низ плиты), не замерено (К-2); толщины стен приняты: наружные 260 мм, перегородки 130 мм (К-1); положение стен и проёмов — по брифу без обмера и плана БТИ (К-1); разрешённая мощность 10 кВт принята, ТУ не переданы (К-6); вентканалы приняты, в брифе не заданы (К-5); тип дома, перекрытие и несущие стены не известны — документов нет (К-3); плита электрическая — принята, в брифе не указано (К-6); система заземления TN-C-S принята, ТУ не переданы (К-6); число жильцов 2 принято, в брифе не указано (К-9); подрайон климата не задан — принят не северный (жилые от 2,5 м) (К-26).

Знак «**» — предложение проектировщика, заказчиком не утверждено (согласовать с заказчиком): ЩС — щит слаботочный: место и состав.

См. лист открытых вопросов (лист 5, записи К-1, К-3, К-5, К-6, К-9; лист 6, запись К-26).

Изм.	Кол.уч	Лист	№ док.	Подп.	Дата
Разраб.		Кырлан А.С.			04.11.26
Пров.					
ГИП					
Н. контр.					
Утв.					

ГД-2026-020-АИ

Квартира 68 м², элитный модерн

Общая площадь 68,47* м² · * размеры приняты, не замерены (реестр — л. 5–7, К-1)

Дизайн-проект интерьера

Стадия	Лист	Листов
РП	101	105

Ведомость объёмов работ (окончание)

М б/м

Кырлан Александр Сергеевич

Спецификация материалов

Отделочные материалы: чистое количество, запас, упаковка, к заказу · ГОСТ 21.110-2013

ПРЕДВАРИТЕЛЬНО · не для производства работ · открыто пунктов: 25 (реестр — л. 5–7)

Спецификация материалов (ГОСТ 21.110-2013, форма 1)

Поз.	Наименование и техническая характеристика	Тип, марка, артикул	Код продукции	Поставщик	Ед. изм.	Количество				Масса ед., кг	Примечание
						чистое	запас, %	упаковка	к заказу		
Покрытия полов и облицовка											
1	Инженерная доска (дуб натуральный, рабочий слой 4 мм, эмиссия E1, прямая укладка)	аналог: инженерная доска, дуб натуральный, масло, 1-полосная, 14/4 мм			м²	49,02	7	по артикулу	52,50 м²		пом. 1, 5, 6, 7; до целой упаковки; л. 53–55
2	Клей для паркетной и инженерной доски (эластичный, по ТУ изготовителя доски)	по выбору подрядчика			м²	49,02		ведро по ТУ	по ТУ		расход кг/м² — по ТУ клея; л. 53
3	Керамогранит 600×600 мм под травертин	аналог: керамогранит под травертин			шт	18	10	коробка	21 шт		2 целых + 16 с подрезкой; 5,81 м² по раскладке, к заказу 7,56 м²; пом. 2, 3; л. 49–52
4	Керамогранит 600×1200 мм под травертин	аналог: керамогранит под травертин			шт	52	10	коробка	61 шт		13 целых + 39 с подрезкой; 30,23 м² по раскладке, к заказу 43,92 м²; пом. 2, 3; л. 49–52
5	Керамогранит 600×1200 мм ректифицированный под травертин, матовый	аналог: керамогранит ректифицированный под травертин, матовый			шт	24	10	коробка	27 шт		8 целых + 16 с подрезкой; 13,87 м² по раскладке, к заказу 19,44 м²; пом. 4; л. 49–52
6	Керамогранит 1200×600 мм под травертин, матовый	аналог: керамогранит под травертин, матовый			шт	5	10	коробка	6 шт		0 целых + 5 с подрезкой; 1,68 м² по раскладке, к заказу 4,32 м²; пом. 5; л. 49–52
Сухие смеси и гидроизоляция											
7	Клей плиточный цементный класса C2 TE S1 (ГОСТ Р 56387-2018)	Ceresit CM 17 или аналог			кг	373,61	10	мешок 25 кг	17 меш.	25	слой 5 мм, 1,50 кг/м² на 1 мм; л. 49
8	Затирка цементная класса CG2WA, цвет — по колерной карте	Mapei Ultracolor Plus 132 или аналог			кг	3,71	10	упак. 2 кг	3 упак.	2	расход (a+b)/ab × шов × t × 1,6 кг/м²; л. 49
9	Гидроизоляция обмазочная полимерная, 2 слоя, лента в углах, манжеты на выводах	по выбору подрядчика			м²	14,32	10	ведро по ТУ	по ТУ		пом. 2, 3; расход кг/м² — по ТУ; л. 49
10	Лента демпферная по периметру пола из плитки	по выбору подрядчика			м	24,41	10	рулон	27,00 м		л. 49
11	Смесь цементно-песчаная для стяжки М200 (50 мм, 33 мм)	по выбору подрядчика			м³	3,36	5	мешок по ТУ	по ТУ		S 69,26 м² × толщина; армирование и маяки — по ТУ; л. 53
12	Смесь штукатурная гипсовая для машинного и ручного нанесения по маякам, слой до 10 мм	по выбору подрядчика			м²	191,15	10	мешок по ТУ	по ТУ		пом. 1, 2, 3, 4, 5, 6, 7; расход кг/м² на 1 мм слоя — по ТУ смеси, толщина — по замеру кривизны стен; л. 15, 54, 55
Короба из ГКЛВ											
13	Лист ГКЛВ 12,5 мм, 2500 × 1200 мм, обшивка коробов в 2 слоя	по выбору подрядчика			м²	2,94	10	лист 3,00 м²	2,00 лист		инсталляция пом. 2: 1,47 м²; площадь × 2 слоя; короб К1 над полом — в спецификации ВК; л. 34, 49–52
14	Профиль стальной оцинкованный 27 × 28 мм: каркас коробов (стойки и направляющие)	по выбору подрядчика			м	7,00	10	хлыст 3 м	3 шт		стойки через 400 мм по свободному периметру + направляющие по полу и потолку; крепёж, лента, шпаклёвка швов — по узлу короба; л. 34, 49–52
Слаботочные сети											
15	Кабель домофона — тип по системе поставщика	по выбору подрядчика			м	3,10		бухта по ТУ	4,00 м		по лучам от ЩС**, 1 точ., запас 10 % уже в длине; 1 точ. — предложение листа слаботочки (знак «*» на плане); л. 31
16	Кабель коаксиальный RG-6 (75 Ом) к розеткам ТВ	по выбору подрядчика			м	14,10		бухта по ТУ	15,00 м		по лучам от ЩС**, 1 точ., запас 10 % уже в длине; 1 точ. — предложение листа слаботочки (знак «*» на плане); л. 31
17	Кабель U/UTP кат. 5e (LAN, Wi-Fi и камеры по PoE)	по выбору подрядчика			м	27,40		бухта по ТУ	28,00 м		по лучам от ЩС**, 2 точ., запас 10 % уже в длине; 1 точ. — предложение листа слаботочки (знак «*» на плане); л. 31
18	Кабель U/UTP кат. 6 (LAN, Wi-Fi и камеры по PoE)	по выбору подрядчика			м	2,70		бухта по ТУ	3,00 м		по лучам от ЩС**, 1 точ., запас 10 % уже в длине; 1 точ. — предложение листа слаботочки (знак «*» на плане); л. 31
19	Гофротруба Ø20 для слаботочных линий, отдельно от силовых	по выбору подрядчика			м	42,60		бухта по ТУ	43,00 м		по длине лучей без участков в канале плинтуса (≈ 90 %); л. 31

Допущения и предложения на листе

Основа листа: планировка по обводу плана заказчика, не замерена (К-1); высота до плиты 2650 мм от чистого пола — решение автора (ИЗ-1); отметки плана потолков сдвинуты на -95 мм (+2.745 плана = низ плиты), не замерено (К-2); толщины стен приняты: наружные 260 мм, перегородки 130 мм (К-1); положение стен и проёмов — по брифу без обмера и плана БТИ (К-1); разрешённая мощность 10 кВт принята, ТУ не переданы (К-6); вентканалы приняты, в брифе не заданы (К-5); тип дома, перекрытие и несущие стены не известны — документов нет (К-3); плита электрическая — принята, в брифе не указано (К-6); система заземления TN-C-S принята, ТУ не переданы (К-6); число жильцов 2 принято, в брифе не указано (К-9); подрайон климата не задан — принят не северный (жилые от 2,5 м) (К-26).

Знак «**» — предложение проектировщика, заказчиком не утверждено (согласовать с заказчиком): ЩС — щит слаботочный: место и состав; К-7: акцент пом. 1, 5–7; К-8: пол пом. 1, 4–7, плинтус пом. 1, 4–7, стены пом. 2, 3, фартук пом. 5 — артикул изделия не выбран: позиция описана характеристиками («аналог по характеристикам»), артикул выбирается при закупке; пол пом. 2, 3 — пирог пола: стяжка 33 мм и обмазочная гидроизоляция добавлены разработчиком проекта; артикул изделия не выбран: позиция описана характеристиками («аналог по характеристикам»), артикул выбирается при закупке.

См. лист открытых вопросов (лист 5, записи К-1, К-3, К-5–К-9; лист 6, запись К-26).

Изм.	Кол.уч	Лист	№ док.	Подп.	Дата
Разраб.		Кырлан А.С.			04.11.26
Пров.					
ГИП					
Н. контр.					
Утв.					

ГД-2026-020-АИ

Квартира 68 м², элитный модерн

Общая площадь 68,47* м² · * размеры приняты, не замерены (реестр — л. 5–7, К-1)

Дизайн-проект интерьера

Стадия	Лист	Листов
РП	102	105

Спецификация материалов

М б/м

Кырлан Александр Сергеевич

Спецификация материалов (окончание)

Отделочные материалы: чистое количество, запас, упаковка, к заказу · ГОСТ 21.110-2013

Спецификация материалов (ГОСТ 21.110-2013, форма 1) (продолжение)

Поз.	Наименование и техническая характеристика	Тип, марка, артикул	Код продукции	Поставщик	Ед. изм.	Количество				Масса ед., кг	Примечание
						чистое	запас, %	упаковка	к заказу		
20	Розетка компьютерная RJ45, кат. 6, с рамкой и подрозетником	по выбору подрядчика			шт	2		шт	2 шт		LAN1, LAN2; серия механизмов — как у розеток и выключателей; л. 26, 27, 31
21	Розетка телевизионная (коаксиальная) с рамкой и подрозетником	по выбору подрядчика			шт	1		шт	1 шт		ТВ1; серия механизмов — как у розеток и выключателей; л. 26, 27, 31
22	Трубка или монитор домофона (поставка домофонной организации)	по выбору подрядчика			шт	1		шт	1 шт		ДФ1; серия механизмов — как у розеток и выключателей; л. 26, 27, 31
23	Щит слаботочный ЩС**: корпус, DIN-рейка, розетки 220 В	по выбору подрядчика			шт	1		шт	1 шт		ЩС**; серия механизмов — как у розеток и выключателей; л. 26, 27, 31
24	Патч-панель, портов не менее 3	по выбору подрядчика			шт	1		шт	1 шт		серия механизмов — как у розеток и выключателей; л. 26, 27, 31
Лакокрасочные материалы											
25	Краска интерьерная акриловая, матовая, класс истирания 1	Tikkurila Euro Power 7, колеровка по NCS No. 30 «Hague Blue — глубокий сине-зелёный»			л	2,30	10	банка 2,7 л	1 банк		9,60 м² × 2 сл. × 0,12 л/м²; пом. 1; л. 54, 55
26	Краска интерьерная акриловая, матовая, класс истирания 1	Farrow & Ball Modern Emulsion No. 2003 «Pointing»			л	27,84	10	банка 2,5 л	13 банк		115,99 м² × 2 сл. × 0,12 л/м²; пом. 1, 4, 5, 6, 7; л. 54, 55
27	Краска интерьерная акриловая, глубокоматовая, класс истирания 2	Tikkurila Euro Power 7 G503 «Calla»			л	15,04	10	банка 2,7 л	7 банк		62,66 м² × 2 сл. × 0,12 л/м²; пом. 1 (пот.), 4 (пот.), 5 (пот.), 6 (пот.), 7 (пот.); л. 54, 55
28	Краска интерьерная акриловая, матовая, класс истирания 1	Tikkurila Euro Power 7 G503 «Calla»			л	1,39	10	банка 2,7 л	1 банк		5,81 м² × 2 сл. × 0,12 л/м²; пом. 2 (пот.), 3 (пот.); л. 54, 55
29	Краска интерьерная акриловая, матовая, класс истирания 1	Tikkurila Euro Power 7, колеровка по NCS No. 281 «Stiffkey Blue — чернильный синий»			л	2,39	10	банка 2,7 л	1 банк		9,96 м² × 2 сл. × 0,12 л/м²; пом. 5; л. 54, 55
30	Краска интерьерная акриловая, матовая, класс истирания 1	Farrow & Ball Modern Emulsion No. 43 «Eating Room Red — брусничный красный»			л	2,38	10	банка 2,5 л	2 банк		9,92 м² × 2 сл. × 0,12 л/м²; пом. 6; л. 54, 55
31	Краска интерьерная акриловая, матовая, класс истирания 1	Farrow & Ball Modern Emulsion No. 34 «Calke Green — традиционный шалфей»			л	3,11	10	банка 2,5 л	2 банк		12,95 м² × 2 сл. × 0,12 л/м²; пом. 7; л. 54, 55
32	Шпаклёвка финишная полимерная под окраску (стены и потолки, Q3)	по выбору подрядчика			м²	226,89	10	ведро по ТУ	по ТУ		расход кг/м² на слой — по ТУ; л. 54, 55
33	Грунтовка акриловая глубокого проникновения, 2 слоя	по выбору подрядчика			м²	259,62	10	канистра по ТУ	по ТУ		расход л/м² — по ТУ; л. 54, 55
Погонажные изделия и потолки											
34	Плинтус напольный МДФ под покраску, h=80 мм, крепление к стене	аналог: плинтус МДФ под покраску 80×16			м.п.	63,89	10	хлыст 2,4 м	30 шт		пом. 1, 4, 5, 6, 7; длина хлыста — по артикулу; л. 54, 55
35	Потолок подвесной ГКЛ/ГКЛВ по каркасу Knauf П113: листы, профили, подвесы, лента, шпаклёвка швов	Knauf П113			м²	68,04		комплект	по л. потолков		площадь — по ведомости потолков; число листов, профилей и подвесов — по шагам каркаса на листе потолков; л. 45–48
Инженерные изделия											
36	Мат нагревательный электрический для тёплого пола под плитку, с холодным концом и муфтой	по выбору подрядчика (мощность — по контурам)			м²	3,00		мат по контуру	по контурам		пом. 3: 1,06 м², 160 Вт; пом. 4: 1,94 м², 290 Вт; типоразмер мата подбирается под контур — нагревательную жилу резать нельзя; л. 23, 53
37	Терморегулятор тёплого пола с выносным датчиком пола, монтаж в подрозетник	по выбору подрядчика			шт	2		шт	2 шт		датчик — в гофротрубе с доступом для замены; по одному на контур; л. 23

Примечания

1. Чистое количество — из ведомости объёмов работ и раскладки плитки; запас — отдельной графой (доска — по ведомости отделки, плитка, краска и плинтус — 10 %); «к заказу» — с запасом и кратно упаковке.
2. Плитка — штуками по раскладке, запас на каждую поверхность. Калибр (рабочий размер) и тон — одной партией на помещение, калибр указать при заказе и сверить с раскладкой до укладки.
3. Краска — 0,12 л/м² на слой (середина вилки 0,10–0,15 л/м²) по фактической площади окраски из ведомости отделки; колеровка одной партией.
4. «По ТУ» — расход задаёт производитель выбранного продукта; количество к заказу — после выбора марки.
5. Поз. 1, 3, 4, 5, 6, 34 заданы характеристиками («аналог:»): марку, артикул и поставщика согласовать с заказчиком до закупки, без артикула не заказывать.
6. Штукатурная смесь — на ту же площадь, что строка ВОР «Штукатурка стен» (191,15 м²): площадь одна, расход смеси задаёт производитель.
7. Коробы инсталляции и стояков: ГКЛВ в 2 слоя и профиль 27 × 28 мм считаются по свободным граням коробов (источник — раскладка плиточника и шахты в данных); короб К1 над полом — в спецификации ВК.
8. Потолки ГКЛ: в этой спецификации — площадь системы П113; число листов, профилей и подвесов — по шагам каркаса на листе потолков (подвесы через 1000, несущие через 500, основные через 1200 мм), схема каркаса не выпущена. Сантехника, светильники и мебель — по своим спецификациям.

Допущения и предложения на листе. Основа листа: планировка по обводу плана заказчика, не замерена (К-1); высота до плиты 2650 мм от чистого пола — решение автора (ИЗ-1); отметки плана потолков сдвинуты на -95 мм (+2.745 плана = низ плиты), не замерено (К-2); толщины стен приняты: наружные 260 мм, перегородки 130 мм (К-1); положение стен и проёмов — по брифу без обмера и плана БТИ (К-1); разрешённая мощность 10 кВт принята, ТУ не переданы (К-6); вентканалы приняты, в брифе не заданы (К-5); тип дома, перекрытие и несущие стены не известны — документов нет (К-3); плита электрическая — принята, в брифе не указано (К-6); система заземления TN-C-S принята, ТУ не переданы (К-6); число жильцов 2 принято, в брифе не указано (К-9); подрайон климата не задан — принят не северный (жилые от 2,5 м) (К-26). Знак «**» — предложено, не утверждено (согласовать): ЩС; К-7: акцент пом. 1, 5–7; К-8: пол пом. 1–7, плинтус пом. 1, 4–7, стены пом. 2, 3, фартук пом. 5. См. лист открытых вопросов (лист 5, записи К-1, К-3, К-5–К-9; лист 6, запись К-26).

Изм.	Кол.уч	Лист	№ док.	Подп.	Дата
Разраб.		Кырлан А.С.			04.11.26
Пров.					
ГИП					
Н. контр.					
Утв.					

ГД-2026-020-АИ

Квартира 68 м², элитный модерн

Общая площадь 68,47* м² · * размеры приняты, не замерены (реестр — л. 5–7, К-1)

Дизайн-проект интерьера	Стадия	Лист	Листов
	РП	103	105

Спецификация материалов (окончание)

М б/м

Кырлан Александр Сергеевич

выпуск 04.11.2026 № 8be4ef4c81 · стр. 113 из 117

Смета ориентировочная

ПРЕДВАРИТЕЛЬНО · не для производства работ · открыто пунктов: 25 (реестр — л. 5–7)

Работы, материалы, оборудование, услуги и резерв · цены — ориентир по открытым прайсам, не коммерческое предложение

Сводная смета (прайсы собраны 21.09.2026, часть расценок сверена повторно 24.09.2026, Москва)

№	Наименование работ, материалов, услуг	Ед. изм.	Кол-во	Цена за ед., ₽	Стоимость, ₽			Чей подряд	Срок поставки, дн.	Основание	Источник цены
					план	факт	разница				
Работы — по ведомости объёмов работ											
1	Демонтаж и черновые работы (без 5 поз. по КП)	раздел	1		248 401			бригада		ВОР, поз. 1–10; л. 99–101	по ВОР
2	Инженерные системы (без 12 поз. по КП)	раздел	1		174 430			бригада		ВОР, поз. 11–35; л. 99–101	по ВОР
3	Чистовые работы (без 1 поз. по КП)	раздел	1		559 457			бригада, поставщик		ВОР, поз. 36–53; л. 99–101	по ВОР
Материалы — по спецификации материалов											
4	Инженерная доска	м²	52,50	4 513	236 933			поставщик		спецификация, поз. 1	Ц7
5	Керамогранит 600×600 мм	м²	7,56	1 800	13 608			поставщик		спецификация, поз. 3	Ц6
6	Керамогранит 600×1200, 1200×600 мм	м²	67,68	3 500	236 880			поставщик		спецификация, поз. 4, 5, 6	Ц6
7	Клей плиточный цементный класса C2 TE S1	меш.	17	1 800	30 600			поставщик		спецификация, поз. 7	Ц7
8	Затирка цементная класса CG2WA	упак.	3	1 000	3 000			поставщик		спецификация, поз. 8	Ц7
9	Краска Tikkurila (Euro Power 7, колеровка по NCS, Euro Power 7), банка 2,7 л	банк	10	3 510	35 100			поставщик		спецификация, поз. 25, 27, 28, 29	Ц6
10	Краска Farrow & Ball Modern Emulsion, банка 2,5 л	банк	17	5 800	98 600			поставщик		спецификация, поз. 26, 30, 31	Ц7
11	Плинтус напольный МДФ под покраску	шт	30	368	11 040			поставщик		спецификация, поз. 34	Ц7
12	Прочие материалы с расходом по ТУ (клей для доски, гидроизоляция, демпферная лента, смесь для стяжки, смесь штукатурная гипсовая для машинного и ручного нанесения по маякам, лист гклв 12, профиль стальной оцинкованный 27 × 28 мм: каркас коробов (стойки и направляющие), кабель слаботочки, гофра слаботочки, изделия слаботочки, шпаклёвка, грунтовка, каркас и ГКЛ потолков, мат нагревательный электрический для тёплого пола под плитку, терморегулятор тёплого пола с выносным датчиком пола)	компл	1	по КП				поставщик		спецификация, поз. 2, 9, 10, 11, 12, 13, 14, 15, 16, 17, 18, 19, 20, 21, 22, 23, 24, 32, 33, 35, 36, 37	
Оборудование и мебель — поставка по спецификациям											
13	Кухонный гарнитур по проекту кухни, изготовление и монтаж (4–8 нед.)	компл	1	по КП				поставщик	не задан; ориентир 4–8 нед. от замера	л. 66, 67	
14	Двери межкомнатные, поставка	шт	6	по КП				поставщик		л. 17	

Допущения и предложения на листе

Основа листа: планировка по обводу плана заказчика, не замерена (К-1); высота до плиты 2650 мм от чистого пола — решение автора (ИЗ-1); отметки плана потолков сдвинуты на -95 мм (+2.745 плана = низ плиты), не замерено (К-2); толщины стен приняты: наружные 260 мм, перегородки 130 мм (К-1); положение стен и проёмов — по брифу без обмера и плана БТИ (К-1); разрешённая мощность 10 кВт принята, ТУ не переданы (К-6); вентканалы приняты, в брифе не заданы (К-5); тип дома, перекрытие и несущие стены не известны — документов нет (К-3); плита электрическая — принята, в брифе не указано (К-6); система заземления TN-C-S принята, ТУ не переданы (К-6); число жильцов 2 принято, в брифе не указано (К-9); подрайон климата не задан — принят не северный (жилые от 2,5 м) (К-26).

Открытые вопросы и конфликты по листу: К-23.

См. лист открытых вопросов (лист 5, записи К-1, К-3, К-5, К-6, К-9; лист 6, записи К-23, К-26).

Изм.	Кол.уч	Лист	№ док.	Подп.	Дата
Разраб.		Кырлан А.С.			04.11.26
Пров.					
ГИП					
Н. контр.					
Утв.					

ГД-2026-020-АИ

Квартира 68 м², элитный модерн

Общая площадь 68,47* м² · * размеры приняты, не замерены (реестр — л. 5–7, К-1)

Дизайн-проект интерьера

Стадия	Лист	Листов
РП	104	105

Смета ориентировочная

М б/м

Кырлан Александр Сергеевич

Смета ориентировочная (окончание)

ПРЕДВАРИТЕЛЬНО · не для производства работ · открыто пунктов: 25 (реестр — л. 5–7)

Работы, материалы, оборудование, услуги и резерв · цены — ориентир по открытым прайсам, не коммерческое предложение

Сводная смета (прайсы собраны 21.09.2026, часть расценок сверена повторно 24.09.2026, Москва) (продолжение)

№	Наименование работ, материалов, услуг	Ед. изм.	Кол-во	Цена за ед., ₽	Стоимость, ₽			Чей подряд	Срок поставки, дн.	Основание	Источник цены
					план	факт	разница				
15	Оборудование заказчика слаботочных сетей: точка доступа wi-fi — 1 шт; коммутатор — 1 шт	компл	1	по КП				заказчик		л. 26, 27	
16	Сантехника, светильники, мебель и предметы интерьера	компл	1	по КП				поставщик		л. 43; л. 44; л. 69; л. 20–22	
Прочие работы и услуги											
17	Вынос и вывоз строительного мусора	м³		по факту				бригада		после демонтажа	
18	Подъём материалов на этаж (лифтом или вручную — по договору)	т		по факту				бригада		по массе поставки	
19	Доставка чистовых материалов, 10 % от поставки			10 %	66 576			поставщик		от суммы материалов	
20	Уборка после ремонта	м²	68,47	по факту				бригада		S квартиры	
	Итого работы				**982 288**						
	Итого материалы				**665 761**						
	Итого прочие услуги				**66 576**						
	Резерв на непредвиденные работы и материалы, 15 %				**257 194**						
	ВСЕГО ориентировочно (без оборудования и позиций по КП)				**1 971 819**						

Примечания

1. Смета ориентировочная, не коммерческое предложение: объёмы — из ведомости объёмов работ и спецификации материалов, цены — нижняя граница открытых прайсов Москвы (прайсы собраны 21.09.2026, часть расценок сверена повторно 24.09.2026); перед договором цены подтвердить у подрядчика и поставщиков.
2. Источники цен: Ц1 — Домашний мастерок: прайс на отделочные работы, 2026; Ц2 — Домашний мастерок: прайс на плиточные работы, 2026; Ц3 Домашний мастерок: прайс на электромонтажные работы, 2026; Ц4 — Профи ремонтник: штукатурно-малярные работы; Ц5 — Profi.ru: укладка керамогранита на стены, Москва 2026; Ц6 — knowledge/spec-materials.md, разд. 1 и 3: ориентир по сегментам; Ц7 — Розница Москвы, 09.2026: Леманa ПРО, KGSnab, официальный дилер Farrow & Ball.
3. Повторная сверка с прайсом: 24.09.2026 — тёплые полы, регулятор тёплых полов; остальные расценки — по прайсам, собранным 21.09.2026.
4. В итог не вошли позиции «по КП» и «по факту»: оборудование и мебель, двери, материалы с расходом по ТУ, вывоз мусора, подъём и уборка.
5. Доставка — 10 % от материалов, резерв — 15 % (частный ремонт 10–20 %) отдельными строками, в количествах не спрятаны. Графы «факт» и «разница» заполняются по актам.

Допущения и предложения на листе

Основа листа: планировка по обводу плана заказчика, не замерена (К-1); высота до плиты 2650 мм от чистого пола — решение автора (ИЗ-1); отметки плана потолков сдвинуты на -95 мм (+2.745 плана = низ плиты), не замерено (К-2); толщины стен приняты: наружные 260 мм, перегородки 130 мм (К-1); положение стен и проёмов — по брифу без обмера и плана БТИ (К-1); разрешённая мощность 10 кВт принята, ТУ не переданы (К-6); вентканалы приняты, в брифе не заданы (К-5); тип дома, перекрытие и несущие стены не известны — документов нет (К-3); плита электрическая — принята, в брифе не указано (К-6); система заземления TN-C-S принята, ТУ не переданы (К-6); число жильцов 2 принято, в брифе не указано (К-9); подрайон климата не задан — принят не северный (жилые от 2,5 м) (К-26).
См. лист открытых вопросов (лист 5, записи К-1, К-3, К-5, К-6, К-9; лист 6, запись К-26).

Изм.	Кол.уч	Лист	№ док.	Подп.	Дата
Разраб.		Кырлан А.С.			04.11.26
Пров.					
ГИП					
Н. контр.					
Утв.					

ГД-2026-020-АИ

Квартира 68 м², элитный модерн

Общая площадь 68,47* м² · * размеры приняты, не замерены (реестр — л. 5–7, К-1)

Дизайн-проект интерьера

Стадия	Лист	Листов
РП	105	105

Смета ориентировочная (окончание)

М б/м

Кырлан Александр Сергеевич

11

Визуализации

Кырлан Александр Сергеевич

выпуск 04.11.2026 № 8be4ef4c81 · стр. 116 из 117



Санузел

Квартира 68 м², элитный модерн · визуализация 1 из 1

выпуск 04.11.2026 № 8be4ef4c81 · стр. 117 из 117