ПРЕДВАРИТЕЛЬНО · не для производства работ · открыто пунктов: 10 (реестр — л. 6, 7)

L

LINEA

ДИЗАЙН-ПРОЕКТ ИНТЕРЬЕРА

Квартира 55 м²

кухня-гостиная и спальня



ПАЛИТРА ОТДЕЛКИ

NCS S 1502-Y50	NCS S 1002-Y50	V503
44 %	32 %	24 %

АВТОР ПРОЕКТА

Кырлан Александр Сергеевич

Ноябрь 2026



План расстановки мебели · М 1:50

ОБЩАЯ ПЛОЩАДЬ	ПОМЕЩЕНИЙ	СТАДИЯ	ШИФР	ОСНОВА
55,23 м²	6, из них жилых 2	Рабочий проект · предварительно	ГД-2026-006-АИ	план заказчика, без обмера

Изм.	Кол.уч	Лист	№ док.	Подп.	Дата
Разраб.		Кырлан А.С.			04.11.26
Пров.					
ГИП					
Н. контр.					
Утв.					

ГД-2026-006-АИ

Квартира 58 м²

Общая площадь 55,23* м² · * размеры приняты, не замерены (реестр — л. 6, 7, К-5)

Дизайн-проект интерьера

Стадия	Лист	Листов
РП	1	87

Титульный лист

М б/м

Кырлан Александр Сергеевич

выпуск 04.11.2026 № 94e55e632e · стр. 1 из 96

Общие данные

ПРЕДВАРИТЕЛЬНО · не для производства работ · открыто пунктов: 10 (реестр — л. 6, 7)

Комплект ГД-2026-006-АИ · Квартира 58 м² · кухня-гостиная и спальня

Допущения и предложения на листе. См. лист открытых вопросов (листы 6, 7).

Ведомость рабочих чертежей основного комплекта ГД-2026-006-АИ

Лист	Наименование	Примечание
1	Титульный лист	
2	Общие данные	
3	Общие данные	
4	Общие данные	
5	Общие данные	
6	Открытые вопросы, принятые допущения и конфликты. Лист 1 из 2	
7	Открытые вопросы, принятые допущения и конфликты. Лист 2 из 2	
8	Задание на контрольный обмер и обследование. Лист 1 из 3	
9	Задание на контрольный обмер и обследование. Лист 2 из 3	
10	Задание на контрольный обмер и обследование. Лист 3 из 3	
11	График закупок и работ. Лист 1 из 3	
12	График закупок и работ. Лист 2 из 3	
13	График закупок и работ. Лист 3 из 3	
14	Обмерный план	
15	План демонтажа и монтажа перегородок	
16	План дверей и ведомость заполнения проёмов	
17	Концепция интерьера	
18	План расстановки мебели	
19	Спецификация мебели и оборудования	
20	План розеток и электровыводов	
21	План освещения	
22	План выключателей и схема включения	
23	Ведомость электроточек и изделий	
24	Однолинейная схема щита	
25	План принципиальных трасс	
26	План слаботочных сетей	
27	План вентиляции	
28	План отопления	
29	План выводов сантехники	
30	Схема разводки водопровода и канализации	

Ведомость рабочих чертежей основного комплекта ГД-2026-006-АИ (продолжение)

Лист	Наименование	Примечание
31	Аксонометрическая схема В1 (холодное водоснабжение)	
32	Аксонометрическая схема Т3 (горячее водоснабжение)	
33	Аксонометрическая схема К1 (канализация)	
34	Развёртки мокрых зон: выводы ВК. Кухня-гостиная	
35	Развёртки мокрых зон: выводы ВК. Ванная (лист 1 из 2)	
36	Развёртки мокрых зон: выводы ВК. Ванная (лист 2 из 2)	
37	Развёртки мокрых зон: выводы ВК. Санузел	
38	Спецификация сантехнического оборудования	
39	Техническое задание на подбор светильников	
40	План потолков	
41	Разрезы и узлы потолков	
42	Разрезы и узлы потолков (продолжение)	
43	Раскладка плитки. Планы полов	
44	Раскладка плитки. Прихожая	
45	Раскладка плитки. Ванная. Развёртки стен	
46	Раскладка плитки. Санузел. Развёртки стен	
47	План полов	
48	Ведомость отделки помещений	
49	Колерная карта	
50	Спецификация отделочных материалов	
51	Концепция декора и визуализации	
52	Встроенная мебель. Схема расположения	
53	Шкаф-купе М9	

Общие указания — лист 5: ±0,000 — чистый пол; несущие конструкции и сети дома — по отдельному проекту; скрытые работы — по актам. Открытые вопросы и допущения — листы 6, 7.

Изм.	Кол.уч	Лист	№ док.	Подп.	Дата	ГД-2026-006-АИ		
						Квартира 58 м²		
						Общая площадь 55,23* м² · * размеры приняты, не замерены (реестр — л. 6, 7, К-5)		
Разраб.		Кырлан А.С.			04.11.26	Дизайн-проект интерьера	Стадия: РП	Лист: 2 / Листов: 87
Пров.								
ГИП						Общие данные	Кырлан Александр Сергеевич	
						М б/м		
Н. контр.								
Утв.								

выпуск 04.11.2026 № 94e55e632e · стр. 2 из 96

Общие данные

Комплект ГД-2026-006-АИ · лист 2 общих данных (продолжение)

Ведомость рабочих чертежей основного комплекта ГД-2026-006-АИ (продолжение)

Лист	Наименование	Примечание
54	Система хранения Г1	
55	Кухня (пом. 1). Развёртка гарнитура	
56	Кухня (пом. 1). Монтажная схема	
57	Шкафы. Монтажная схема	
58	Ведомости изделий, техники и фурнитуры	
59	Реестр марок отделки и позиций альбома	
60	Схема расположения развёрток и узлов	
61	Развёртка стены В. Кухня-гостиная (пом. 1), кухонный фронт	
62	Привязки электроточек и выводов ВК, стена В. Кухня-гостиная (пом. 1)	
63	Развёртка стены А. Кухня-гостиная (пом. 1)	
64	Развёртка стены Б. Кухня-гостиная (пом. 1)	
65	Развёртка стены Г. Кухня-гостиная (пом. 1)	
66	Развёртка стены А. Спальня (пом. 2)	
67	Развёртка стены Б. Спальня (пом. 2)	
68	Привязки электроточек, стена Б. Спальня (пом. 2)	
69	Развёртка стены В. Спальня (пом. 2)	
70	Развёртки стен А, Б, В. Ванная (пом. 3)	
71	Привязки электроточек и выводов ВК, стена В. Ванная (пом. 3)	
72	Развёртка стены Г. Ванная (пом. 3)	
73	Развёртки стен А, Б, В. Санузел (пом. 4)	
74	Развёртка стены Г. Санузел (пом. 4)	
75	Развёртки стен А, Б. Прихожая (пом. 5)	
76	Развёртки стен В, Г. Прихожая (пом. 5)	
77	Привязки электроточек, стена В. Прихожая (пом. 5)	
78	Развёртки стен А, Б. Гардеробная (пом. 6)	
79	Развёртка стены Г. Гардеробная (пом. 6)	
80	Узлы	
81	Ведомость объёмов работ	
82	Ведомость объёмов работ (продолжение)	
83	Ведомость объёмов работ (окончание)	

Общие указания — лист 5: ±0,000 — чистый пол; несущие конструкции и сети дома — по отдельному проекту; скрытые работы — по актам. Открытые вопросы и допущения — листы 6, 7.

Ведомость рабочих чертежей основного комплекта ГД-2026-006-АИ (продолжение)

Лист	Наименование	Примечание
84	Спецификация материалов	
85	Спецификация материалов (окончание)	
86	Смета ориентировочная	
87	Смета ориентировочная (окончание)	

Допущения и предложения на листе

Основа листа: размеры сняты с плана заказчика, контрольный обмер не выполнен (К-5); высота потолка 2700 мм принята: на плане заказчика не указана (К-5); подрайон климата не задан — принят не северный (жилые от 2,5 м) (К-4); толщины стен приняты: наружные 250 мм, перегородки 120 мм — не обмерены (К-5); разрешённая мощность 15 кВт принята по типовой квартире, технических условий нет (К-6).

См. лист открытых вопросов (лист 6, записи К-4–К-6).

						ГД-2026-006-АИ	
						Квартира 58 м²	
Изм.	Кол.уч	Лист	№ док.	Подп.	Дата	Общая площадь 55,23* м² · * размеры приняты, не замерены (реестр — л. 6, 7, К-5)	
Разраб.		Кырлан А.С.			04.11.26	Дизайн-проект интерьера	Стадия: РП · Лист: 3 · Листов: 87
Пров.							
ГИП						**Общие данные**	Кырлан Александр Сергеевич
Н. контр.						М б/м	
Утв.							

выпуск 04.11.2026 № 94e55e632e · стр. 3 из 96

Общие данные

Комплект ГД-2026-006-АИ · лист 3 общих данных (продолжение)

Ведомость ссылочных и прилагаемых документов

Обозначение	Наименование	Примечание
	Ссылочные документы	
ГОСТ 21.201-2011	СПДС. Условные графические изображения элементов зданий, сооружений и конструкций	
ГОСТ 21.205-2016	СПДС. Условные обозначения элементов санитарно-технических систем	
ГОСТ 21.210-2014	СПДС. Изображения условные графические электрооборудования и проводок на планах	
ГОСТ 2.306-68	ЕСКД. Обозначения графические материалов и правила их нанесения на чертежах	
	Прилагаемые документы	
ГД-2026-006-АИ.В1	Визуализация. Интерьер: Ванная (пом. 3), стена Б	альбом визуализаций
ГД-2026-006-АИ.В2	Визуализация. Интерьер: Ванная (пом. 3), стена В	
ГД-2026-006-АИ.В3	Визуализация. Интерьер: Спальня (пом. 2), стена А	
ГД-2026-006-АИ.В4	Визуализация. Интерьер: Спальня (пом. 2), стена Б	
ГД-2026-006-АИ.В5	Визуализация. Интерьер: Прихожая (пом. 5), стена А	
ГД-2026-006-АИ.В6	Визуализация. Интерьер: Прихожая (пом. 5), стена В	
ГД-2026-006-АИ.В7	Визуализация. Интерьер: Кухня-гостиная (пом. 1), стена Б	
ГД-2026-006-АИ.В8	Визуализация. Интерьер: Кухня-гостиная (пом. 1), стена В	
ГД-2026-006-АИ.В9	Визуализация. Интерьер: Кухня-гостиная (пом. 1), стена Г	
ГД-2026-006-АИ.В10	Визуализация. Интерьер: Гардеробная (пом. 6), общий вид	
ГД-2026-006-АИ.В11	Визуализация. Интерьер: Санузел (пом. 4), общий вид	

Состав дизайн-проекта

Раздел	Состав	Листы
Обложка	Дизайн-проект интерьера; Квартира 58 м²; автор проекта — Кырлан Александр Сергеевич	1 с.
Концепция	Стиль Скандинавский: концепция интерьера, палитра и материалы (колерная карта лист 49)	л. 17
Визуализации	11 изобр.: Ванная, стена Б; Ванная, стена В; Спальня, стена А; Спальня, стена Б; Прихожая, стена А; Прихожая, стена В; Кухня-гостиная, стена Б; Кухня-гостиная, стена В; Кухня-гостиная, стена Г; Гардеробная, общий вид; Санузел, общий вид	В1–В11
Рабочие чертежи	планы, развёртки, узлы (развёртки и узлы — листы 34–37, 60, 70, 73, 75, 76, 78, 80)	л. 1–87
Спецификации и ведомости	оборудование, изделия, отделка, электроточки	л. 16, 19, 23, 38, 48–50, 81–85

Допущения и предложения на листе

Основа листа: размеры сняты с плана заказчика, контрольный обмер не выполнен (К-5); высота потолка 2700 мм принята: на плане заказчика не указана (К-5); подрайон климата не задан — принят не северный (жилые от 2,5 м) (К-4); толщины стен приняты: наружные 250 мм, перегородки 120 мм — не обмерены (К-5); разрешённая мощность 15 кВт принята по типовой квартире, технических условий нет (К-6).

См. лист открытых вопросов (лист 6, записи К-4–К-6).

Общие указания — лист 5: ±0,000 — чистый пол; несущие конструкции и сети дома — по отдельному проекту; скрытые работы — по актам. Открытые вопросы и допущения — листы 6, 7.


Изм.	Кол.уч	Лист	№ док.	Подп.	Дата	ГД-2026-006-АИ		
						Квартира 58 м²		
						Общая площадь 55,23* м² · * размеры приняты, не замерены (реестр — л. 6, 7, К-5)		
Разраб.		Кырлан А.С.			04.11.26	Дизайн-проект интерьера	Стадия: РП	Лист: 4 / Листов: 87
Пров.								
ГИП								
Н. контр.						Общие данные	Кырлан Александр Сергеевич	
Утв.						М б/м		

выпуск 04.11.2026 № 94e55e632e · стр. 4 из 96

Общие данные

Комплект ГД-2026-006-АИ · лист 4 общих данных (продолжение)

Условные обозначения

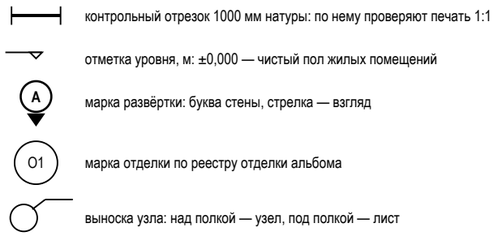

- контрольный отрезок 1000 мм натуры: по нему проверяют печать 1:1
- отметка уровня, м: ±0,000 — чистый пол жилых помещений
- марка развёртки: буква стены, стрелка — взгляд
- марка отделки по реестру отделки альбома
- выноска узла: над полкой — узел, под полкой — лист

Общие указания

1. Рабочие чертежи интерьера разработаны на основании задания на проектирование и обмерного плана (лист 14). Объект: Квартира 58 м²; автор проекта — Кырлан Александр Сергеевич; общая площадь 55,23 м², жилая 34,99 м², помещений 6.
2. Рабочие чертежи выполнены в соответствии с заданием на проектирование и нормативными документами, перечисленными в п. 4.
3. Открытые вопросы, принятые допущения и конфликты между разделами, не снятые к выпуску комплекта, сведены в таблицы на листах 6, 7. До ответа по пункту таблицы показанное на указанном там листе — допущение, а не утверждённое решение: комплект по этим листам предварительный.
4. Нормативные документы, на которые есть ссылки в листах комплекта: ГОСТ Р 21.101-2026; ГОСТ 21.501-2018; ГОСТ 2.302-68; ГОСТ 2.303-68; ГОСТ 2.304-81; ГОСТ 2.307-2011; СП 54.13330.2022; СП 71.13330.2017; СП 73.13330.2016; ПУЭ (7-е изд.), гл. 1.8, 7.1; ГОСТ Р 50571.7.701-2024; СанПиН 1.2.3685-21; ГОСТ 2.702; ГОСТ 2.755; ГОСТ 21.110-2013; ГОСТ 21.601; ГОСТ 13996-2019; ГОСТ 23166-2021; ГОСТ 31173-2016; ГОСТ 31565-2012; ГОСТ 32414-2013; ГОСТ 32415-2013; ГОСТ Р 56387-2018; СП 29.13330.2011; СП 30.13330.2020; СП 51.13330.2011; СП 131.13330. Документы из ведомости ссылочных документов здесь не повторяются.
5. За отметку ±0,000 принят уровень чистого пола жилых помещений квартиры (относительная отметка; абсолютная — по проекту дома). Отметка чистого пола мокрых помещений — −0,015. Размеры — в миллиметрах, отметки — в метрах, площади — в м²; высоты установки Н от чистого пола своего помещения до оси изделия.
6. Несущие конструкции, общедомовые стояки, вентиляционные каналы и инженерные сети дома настоящим комплектом не изменяются. Работы, затрагивающие их (проём или штраба в несущей стене, перенос стояка, врезка в вентканал, расширение мокрой зоны), выполняются только по отдельному проекту, к которому прилагается техническое заключение о допустимости и безопасности работ, выданное автором проекта дома или организацией с допуском на обследование, и который согласован в установленном порядке (Жилищный кодекс РФ, ст. 25–29).
7. Трассы инженерных сетей на листах — принципиальные. Расчёты электрических нагрузок и токов КЗ, гидравлики, воздухообмена, освещённости и нагрузок на перекрытие выполняются в проектах ЭОМ, ВК, ОВ и КР организацией с допуском СРО; фактические трассы до закрытия отделкой фиксируются исполнительными схемами.
8. Стиль интерьера — Скандинавский. Палитра проекта: основной — NCS S 1502-Y50R «S 1502-Y50R», NCS S 1002-Y50R «S 1002-Y50R», NCS S 0300-N «S 0300-N»; дополнительный — Tikkurila V503 «Winter»; акцент — NCS S 4010-R90B «S 4010-R90B». Коды цвета — по веерам производителей; цвет утверждается по выкрасу на объекте при освещении проекта.
9. Площади поверхностей — по чистым граням стен до отделки: стены = периметр × высоту от чистого пола помещения до низа потолка минус проёмы (облицовка плиткой — до верха облицовки); плинтус = периметр минус дверные проёмы; пол и потолок — по площади помещения. Количество плиток — по раскладке. Способ один для всех листов комплекта (ведомость отделки, колерная карта, раскладка плитки, развёртки).
10. Марки: стены помещения на всех листах — А (верхняя по плану), Б (правая), В (нижняя), Г (левая); марка отделки О — одна на весь альбом; реестр марок отделки (с позициями колерной карты той же отделки) и марки позиций по видам — на листе 59.
11. Развёртки стен выполнены по всем помещениям для стен с электроточками, мебелью, декором и отделкой: санузлы и кухонный фронт — в М 1:25, остальные стены — в М 1:25; расположение развёрток и узлов — на листе 60, узлы — на листе 80.
12. Перечень скрытых работ, на которые составляются акты освидетельствования (форма по приказу Минстроя России № 344/пр): гидроизоляция пола и стен мокрых помещений (с тестом проливом); стяжка пола (толщина, прочность, влажность основания); тёплый пол до заливки (сопротивление, схема укладки); скрытая электропроводка (за потолком и в штробах стен; условия штробления — в следующем пункте); трубопроводы водоснабжения и канализации до закрытия (опрессовка, уклоны); закладные и усиления под подвесные приборы, мебель и тяжёлый декор, рамы инсталляций; короба дверей скрытого монтажа до штукатурки; каркасы ГКЛ потолков, коробов и перегородок до обшивки.
13. Скрытая электропроводка: за потолком и в штробах стен. Штробы в стенах выполняются только после технического заключения о несущих конструкциях; до заключения несущие стены не определены, и все стены считаются несущими; объём штроб — в ведомости объёмов работ, строка «Штробы в стенах» (вертикальные спуски; объём не меньше фактического, горизонтальные трассы — по исполнительной схеме).
14. Критерии приёмки: допуски отделочных покрытий — по СП 71.13330.2017; испытания систем водоснабжения и канализации — по СП 73.13330.2016 до закрытия трасс; приёмо-сдаточные испытания электроустановки — по ПУЭ, гл. 1.8, с протоколом электролаборатории.
15. Осознанные отступления от ГОСТ Р 21.101-2026, принятые в комплекте: номер листа и число листов («Листов») указаны на каждом листе; на масштабных листах в основной надписи указан фактический масштаб и дан контрольный отрезок 1000 мм; развёртки стен выполнены в М 1:25 (ГОСТ 21.507-81 — 1:50…1:500) ради читаемости привязок; размерные числа и марки элементов (Д-1, ОК-1, О6) кеглем 2,5 мм, номера помещений — в кружке Ø 8 мм (канон — 3,5 мм и Ø 12 мм): так насыщенные листы А3 читаются без наложений надписей.
16. Графы «Пров.», «Н. контр.», «Утв.» основной надписи заполняются при согласовании комплекта с заказчиком; до согласования комплект подписывает автор проекта (графа «Разраб.»).

Допущения и предложения на листе

Основа листа: размеры сняты с плана заказчика, контрольный обмер не выполнен (К-5); высота потолка 2700 мм принята: на плане заказчика не указана (К-5); подрайон климата не задан — принят не северный (жилые от 2,5 м) (К-4); толщины стен приняты: наружные 250 мм, перегородки 120 мм — не обмерены (К-5); разрешённая мощность 15 кВт принята по типовой квартире, технических условий нет (К-6).

См. лист открытых вопросов (лист 6, записи К-4–К-6).

						ГД-2026-006-АИ	
						Квартира 58 м²	
						Общая площадь 55,23* м² · * размеры приняты, не замерены (реестр — л. 6, 7, К-5)	
Изм.	Кол.уч	Лист	№ док.	Подп.	Дата	Дизайн-проект интерьера	Стадия: РП · Лист: 5 · Листов: 87
Разраб.		Кырлан А.С.			04.11.26		
Пров.							
ГИП							
						Общие данные М б/м	Кырлан Александр Сергеевич
Н. контр.							
Утв.							

выпуск 04.11.2026 № 94e55e632e · стр. 5 из 96

Открытые вопросы, принятые допущения и конфликты. Лист 1 из 2

ПРЕДВАРИТЕЛЬНО · не для производства работ · открыто пунктов: 10 (реестр — л. 6, 7)

Сводка по реестрам координации

Комплект предварительный по пунктам этих таблиц. Пока по пункту нет ответа или решения, показанное на указанном листе — допущение проектировщика, а не утверждённое решение.
Сводка: открытых вопросов — 7 (из них ждут факта объекта — 6: контрольного обмера, обследования или документа); изменений в реестре — 3, из них без подписи — 3.
Пункты, ответ на которые лежит на объекте, а не за столом проектировщика (графа «Вид», строка «Ждёт»), собраны на листе «Задание на контрольный обмер и обследование» (листы 8–10): что и где замерить, с какой точностью и чем подтвердить. Пункты, ждущие решения человека, на объекте не закрываются.

Открытые вопросы и принятые допущения

№	Формулировка	Вид	Кто решает	Если решения нет	Лист, где это проявляется
К-1	Вентканалы на плане заказчика не показаны: ВК-1 принят у перегородки ванной и санузла (со стороны прихожей), ВК-2 — у кухни. От них зависят решётки ВР1–ВР3 и короба. Замерить положение и сечение каналов, проверить тягу.	Отсутствует Ждёт: обмера	Инженер ОВ	решётки ванной и санузла — у ВК-1, кухни — у ВК-2; места — до обмера, лист перевыпустить по факту	л. 27 — План вентиляции
К-2	Ванная (пом. 3), 2140 × 1380 мм в чистоте, проём Д-4 у стены Б. Расстановка проектировщика: ванна 1500 × 700 у стены А от стены Г (была 1600 и заходила в проход перед Д-4 — свободно 240 из 700 мм), умывальник П3 у стены В справа от ванны — перед ним свободно 750 мм (был напротив ванны в 230 мм), полотенцесушитель П5 на стене В между коробом стояков и умывальником. Унитаз П2 из образца раскладки снят: он стоял на стояке Ст К1-1 (короба и люка не поставить), унитаз квартиры — П20 в санузле, инсталляция и короб — там. Остаётся: перед ванной 680 мм до стены В при ориентире 750 мм — это глубина помещения; у умывальника до стены Б 90 мм при ориентире 200 мм. Решить: (а) принять расстановку; (б) душ с поддоном 900 × 900 у стены Г вместо ванны — перед приборами ≥ 750 мм, кадры ванной перерисовать; (в) другой вариант автора.	Спорно Ждёт: решения	Инженер ВК (вода, канализация)	ванна 1500 × 700 и умывальник у стены В по листам; модели ванны и умывальника не заказывать до решения	л. 29 — План выводов сантехники л. 18 — План расстановки мебели
К-3	Скрытые двери Д-2, Д-3, Д-4 стоят в существующих проёмах прихожей, размеров в свету нет: короб скрытой двери шире и выше полотна на 100–120 / 50–80 мм, полотно по проёму 2100 под ряд 2000 не встаёт (по каталогам нужно 2050–2080). У Д-3 (спальня) и Д-4 (санузел) откос от угла 40 мм — под короб нужно не меньше 50. Замерить проёмы в чистоте и откосы; решить: проёмы подрезать/расширить на 10+ мм от угла (если стена не несущая) или взять модель с узким коробом; высоту проёма — по выбранной модели.	Отсутствует Ждёт: обмера, затем решения	Архитектор-планировщик	блоки скрытых дверей не заказывать до замера; полотна на листах — расчётные («расч.»), проёмы не переносятся	л. 16 — План дверей и ведомость заполнения проёмов
К-4	Климатический подрайон (СП 131.13330) не задан: принят не северный — жилые комнаты и кухня под потолком от 2,5 м (СП 54, п. 5.12); в IA, IБ, IГ, IД, IVA — от 2,7 м.	Отсутствует Ждёт: документа	Архитектор-планировщик	отметки потолков жилых — по 2,5 м; при северном подрайоне уровни ниже 2,7 м пересчитать до заказа каркаса	л. 40 — План потолков
К-5	Основа альбома — план заказчика без контрольного обмера: размеры помещений сняты с плана, высота потолка 2700 мм и толщины стен (наружные 250 мм, перегородки 120 мм) приняты — на плане они не указаны. От них зависят вертикальные размеры (развёртки, шкафы, плитка, потолки), объёмы работ и сборка шкафов-купе. Выполнить контрольный обмер.	Непонятно Ждёт: обмера	Архитектор-планировщик	размеры, высота потолка и толщины стен — принятые; мебель на заказ, двери и каркас потолков не заказывать до обмера	л. 14 — Обмерный план
К-6	Разрешённая мощность 15 кВт принята по типовой квартире, технических условий в материалах объекта нет. Сверить с техническими условиями.	Непонятно Ждёт: документа	Инженер-электрик	вводной аппарат и группы щита — по 15 кВт; при меньшей мощности схему щита пересчитать до монтажа	л. 24 — Однолинейная схема щита
К-7	Места стиральной машины в квартире не было. В ванной 2,2 × 1,5 м и санузле места 600 × 600 с подходом нет. Предложение исполнителя: узкая машина 600 × 450 под столешницей кухни вместо модуля с ящиками М11 справа от варочной, ряд удлиняется на 220 мм; отдельная группа щита с УЗО 30 мА. Решить: принять, или машина в ванной вместо ванны (душ), или отказ от машины (прачечная) решением автора	Предложение Ждёт: документа, затем решения	Инженер ВК (вода, канализация)	стиральная машина П6 в кухне под столешницей (ниша вместо М11, 2800…3420) — как на листах	л. 29 — План выводов сантехники л. 18 — План расстановки мебели л. 24 — Однолинейная схема щита

Изм.	Кол.уч	Лист	№ док.	Подп.	Дата
Разраб.		Кырлан А.С.			04.11.26
Пров.					
ГИП					
Н. контр.					
Утв.					

ГД-2026-006-АИ

Квартира 58 м²

Общая площадь 55,23* м² · * размеры приняты, не замерены (реестр — л. 6, 7, К-5)

Дизайн-проект интерьера

Стадия	Лист	Листов
РП	6	87

Открытые вопросы, принятые допущения и конфликты. Лист 1 из 2
М б/м

Кырлан Александр Сергеевич

выпуск 04.11.2026 № 94e55e632e · стр. 6 из 96

Открытые вопросы, принятые допущения и конфликты. Лист 2 из 2

Сводка по реестрам координации

Изменения проекта после выпуска листов (реестр изменений)

№	Дата	Лист	Было	Стало	Кто решил, подпись
ИЗ-1	30.10.2026	л. 20 — План розеток и электровыводов л. 22 — План выключателей и схема включения л. 21 — План освещения л. 58 — Ведомости изделий, техники и фурнитуры	Кухня-гостиная: ТВ1, LAN1 и розетка «ТВ, приставка» стояли на стене В (привязка 3300…3450, кухонная стена), а ТВ-тумба М20 — на стене Г (1500…3300): за телевизором точек не было. Выключатель S1 — на стене Г в зоне экрана, у двери Д-2 выключателя не было. Светильник гардеробной Св16 — на линии L6 подсветки кухонной столешницы, выключателя в гардеробной нет. Ванная и санузел — одна линия L4 с одним выключателем S4. Вытяжка в М10 без вывода питания; розетка холодильника без привязки к модулю М4.	ТВ1 (2400), LAN1 (2550) и розетка приставки (2400, H=300) — на стене Г по оси тумбы М20. S1 стена В, привязка 4950 (150 мм от проёма Д-2 со стороны ручки), S5 у дивана — проходной. Св16 — линия L7, выключатель S8 на стене Г гардеробной у Д-3 (привязка 1500). Санузел — линия L9, выключатель S9 в прихожей у Д-4 санузла (стена Г, привязка 1450); S4 — только ванная (L4, вентилятор ВР2). Розетка вытяжки — стена В привязка 2500, H=2200, группа 2 (для М10); розетка холодильника — для М4.	Не утверждено: подписи нет. решение исполнителя; на утверждение А. С. Кырлана
ИЗ-2	30.10.2026	л. 18 — План расстановки мебели л. 19 — Спецификация мебели и оборудования	Диван М1 на стене Б привязка 1300…3500: торец в 500 мм от стены В, дверь Д-2 (3900…4800) открывалась в торец дивана. Кресло М22 х 4250, у 450.	Диван М1 привязка 1000…3200 — перед проёмом 800 мм; кресло М22 х 3500…4300, у 450 у окна 2. Выключатель S5 и розетка у дивана — привязка 900. Знак «**» у М1, М22 до подписи автора.	Не утверждено: подписи нет. решение исполнителя; предложение проектировщика, на утверждение А. С. Кырлана
ИЗ-3	30.10.2026	л. 27 — План вентиляции	Внутренний блок КВ-1 на стене А привязка 3300…4200 — внутри оконного проёма 3200…4800; наружный КН-1 привязка 3350 — на окне.	КВ-1 — стена Г, привязка 300…1200 (простенок у окна 1), КН-1 — стена А, простенок между окнами 2400…3200. Трасса ≈ 3 м (петля принята по минимуму, паспорта модели нет). Знак «**» у КВ-1 до подписи автора.	Не утверждено: подписи нет. решение исполнителя; предложение проектировщика, на утверждение А. С. Кырлана

Примечания

1. Номера листов — по ведомости рабочих чертежей комплекта (лист «Общие данные»).
2. Графа «Если решения нет» показывает состояние решения на листах; влияние на сроки и стоимость по пунктам не оценивалось.
3. Пункт, по которому принято решение, при следующем выпуске комплекта из таблиц исключается.

Изм.	Кол.уч	Лист	№ док.	Подп.	Дата	ГД-2026-006-АИ		
						Квартира 58 м²		
						Общая площадь 55,23* м² · * размеры приняты, не замерены (реестр — л. 6, 7, К-5)		
Разраб.		Кырлан А.С.			04.11.26	Дизайн-проект интерьера	Стадия: РП	Лист: 7 / Листов: 87
Пров.								
ГИП								
Н. контр.						**Открытые вопросы, принятые допущения и конфликты. Лист 2 из 2** М б/м	**Кырлан Александр Сергеевич**	
Утв.								

выпуск 04.11.2026 № 94e55e632e · стр. 7 из 96

Задание на контрольный обмер и обследование. Лист 1 из 3

ПРЕДВАРИТЕЛЬНО · не для производства работ · открыто пунктов: 10 (реестр — л. 6, 7)

Что замерить, вскрыть и получить до заказа материалов и изделий

Задание собрано из открытых вопросов, ответ на которые лежит на объекте или в документах, а не за столом проектировщика. Пока факт не получен, размер, материал или положение на листах — допущение (знак «*»), а не замер.
Сводка: на объекте — 9 (до демонтажа — 7; после демонтажа — 2); документом и при закупке — 4; из допущений в данных и на листах — 9, из них без вопроса в реестре — 6. Закрываются вопросы: К-1, К-3–К-7 (6). Вопросы, ждущие решения человека, задание не закрывает — они решаются по реестру открытых вопросов.

Условия проведения

Порядок работ	Приёмы и точность	Кто присутствует	Если факт не совпал с проектом
1. До демонтажа — существующее состояние: контур, диагонали, высоты, проёмы, оси стояков, ниши и конструкции, которые видны. 2. После демонтажа, до черновых работ — то, что закрывали отделка и короба: основание стен, фактические толщины, углы, узлы. 3. Документы и данные закупки — не на объекте: к сроку из последней таблицы, от них зависят привязки и заказ. Что заказывается по размеру из задания, до закрытия пункта не заказывают: сроки изготовления — по графику закупок прораба.	Обход по часовой стрелке от входа: стены, проёмы, потолок, коммуникации (стояки, щиток, вентканалы), особенности (ниши, короба, выступы). Размеры записывают в мм; сумма участков равна общему размеру, при цепочке длиннее трёх участков ставят проверочный (общий) размер. Диагонали каждого помещения; если две диагонали различаются на 5 мм и больше, разницу подписывают на плане. Потолок — в нескольких точках: центр, углы, у проёмов. Проём — ширина, высота, глубина откоса, привязка к ближайшим углам, высота подоконника. Допустимая погрешность прибора — 2–3 мм на метр; размеры округляют кратно 5 мм; два контрольных промера одного размера не должны расходиться более чем на 2 %. Допуск по пункту — в графе «Точность». План БТИ обмер не заменяет.	Прораб (отвечает за проведение) — назначает день и порядок обхода, открывает объект и освобождает помещения, ведёт это задание и реестр изменений. Архитектор — выполняет обмер, составляет акт контрольного обмера и подписывает результаты по размерам и конструкциям. Владельцы вопросов присутствуют при пунктах своего раздела или принимают результат до заказа: Инженер ОВ — К-1; позиции О-13, О-3; Инженер-электрик — К-6; позиции О-2; Инженер ВК (вода, канализация) К-7; позиции О-1; Отделочник — позиции О-8, О-9. Заказчик или его представитель — передаёт документы (план БТИ, проект дома, технические условия, паспорта), подписывает акт. Проектных решений на обмере не принимают: обмер даёт факт, решения — по реестру открытых вопросов (листы 6–7).	1. В пределах допуска пункта — принимается измеренное значение, лист перевыпускается, знак «*» снимается. 2. Больше допуска или контрольные промеры расходятся более чем на 2 % — промер повторяют; не подтвердилось — запись в реестр изменений (дата, лист, было, стало, кто решил, подпись), работы в этом месте не начинают. 3. Затронуты несущая стена, стояк, вентканал или мокрая зона — сразу владельцу раздела и ГИПу (главному инженеру проекта); между разделами не больше двух кругов, затем решает ГИП. 4. На объекте устно ничего не согласуется: каждое решение — записью в реестр с подписью.

Этап 1. До демонтажа

№	Где	Способ	Что сделать	Кто выполняет	Точность	Что пересчитается в альбоме	Чем подтверждается	Закрывает вопросы реестра
О-1	Ввод В1 и Т3 у стояков; по всей квартире	Обмер	Отключающая арматура и счётчики воды на вводах: положение, тип, пломбы управляющей компании. Альбом ставит их на каждом вводе по практике, в данных их нет.	Архитектор	±5 мм	Узлы ввода в спецификации ВК (краны, фильтры, счётчики); места ввода на плане выводов. Листы: л. 29 — План выводов сантехники л. 38 — Спецификация сантехнического оборудования	акт контрольного обмера; фото с рулеткой и привязкой к стене или углу	Вопроса в реестре нет: Альбом принимает счётчики воды на вводах без осмотра. Результат принимает: Инженер ВК (вода, канализация)
О-2	Вход в квартиру или лестничная клетка; место щита на плане	Обмер	Существующий щиток и счётчик электроэнергии: место и габарит ниши, состояние ввода, марка и сечение вводного кабеля, наличие вводного автомата и УЗО, пломбы.	Архитектор	±5 мм	Ниша и место щита на листах; вводной кабель и аппараты на однолинейной схеме; расстояния до первых групп. Листы: л. 24 — Однолинейная схема щита	акт контрольного обмера; фото с рулеткой и привязкой к стене или углу	Вопроса в реестре нет: Альбом принимает щит и ввод без осмотра. Результат принимает: Инженер-электрик
О-3	у окон	Обмер	Положение стояков отопления (подающий и обратный) от граней стен, диаметры, наличие запорной арматуры; существующие радиаторы: число секций, межосевое расстояние, подводки. В данных стояков отопления нет — лист отопления выводит их условно у откоса окна.	Архитектор	±5 мм	План отопления: места стояков и подводок, привязки радиаторов; подбор радиаторов по теплотехническому расчёту; радиаторы и узлы подключения в ВОР и спецификации. Листы: л. 28 — План отопления	акт контрольного обмера; фото с рулеткой и привязкой к стене или углу	Вопроса в реестре нет: Альбом принимает положение стояков и радиаторов отопления без обмера. Результат принимает: Инженер ОВ
О-4	санузел, ванная, кухня	Обмер	Положение и сечение вентканалов (вентблока), тяга.	исполнитель	±10 мм	план вентиляции, потолки, короба Листы: л. 27 — План вентиляции	акт контрольного обмера	К-1 Результат принимает: Инженер ОВ
О-5	прихожая (пом. 5)	Обмер	Проёмы Д-2, Д-3, Д-4 в чистоте (ширина, высота от чистого пола) и откосы до углов прихожей.	исполнитель	±5 мм	ведомость заполнения проёмов, план дверей Листы: л. 16 — План дверей и ведомость заполнения проёмов	акт контрольного обмера	К-3 Результат принимает: Архитектор

Допущения и предложения на листе
Основа листа: размеры сняты с плана заказчика, контрольный обмер не выполнен (К-5); высота потолка 2700 мм принята: на плане заказчика не указана (К-5); подрайон климата не задан — принят не северный (жилые от 2,5 м) (К-4); толщины стен приняты: наружные 250 мм, перегородки 120 мм — не обмерены (К-5); разрешённая мощность 15 кВт принята по типовой квартире, технических условий нет (К-6).
См. лист открытых вопросов (лист 6, записи К-4–К-6).

Изм.	Кол.уч	Лист	№ док.	Подп.	Дата
Разраб.		Кырлан А.С.			04.11.26
Пров.					
ГИП					
Н. контр.					
Утв.					

ГД-2026-006-АИ

Квартира 58 м²

Общая площадь 55,23* м² · * размеры приняты, не замерены (реестр — л. 6, 7, К-5)

Дизайн-проект интерьера

Стадия	Лист	Листов
РП	8	87

Задание на контрольный обмер и обследование.
Лист 1 из 3
М б/м

Кырлан Александр Сергеевич

выпуск 04.11.2026 № 94e556632e · стр. 8 из 96

Задание на контрольный обмер и обследование. Лист 2 из 3

ПРЕДВАРИТЕЛЬНО · не для производства работ · открыто пунктов: 10 (реестр — л. 6, 7)

Что замерить, вскрыть и получить до заказа материалов и изделий

Этап 1. До демонтажа (продолжение)

№	Где	Способ	Что сделать	Кто выполняет	Точность	Что пересчитается в альбоме	Чем подтверждается	Закрывает вопросы реестра
О-6	По месту	Обмер	Подтвердить на объекте принятое: подрайон климата не задан — принят не северный (жилые от 2,5 м)	Архитектор	±5 мм	Листы, где используется принятая величина. Листы: л. 2–5 — Общие данные	акт контрольного обмера	К-4 Результат принимает: Архитектор
О-7	все помещения квартиры	Обмер	Контрольный обмер всех помещений: стороны, диагонали, проёмы, толщины стен; высота потолка в каждом помещении в нескольких точках (центр, углы, у проёмов). Принято: потолок 2700 мм, стены 250 / 120 мм.	исполнитель	±5 мм	обмерный и монтажный планы, развёртки, план потолков, шкафы, объёмы работ Листы: л. 14 — Обмерный план	акт контрольного обмера	К-5 Результат принимает: Архитектор

Этап 2. После демонтажа, до черновых работ

№	Где	Способ	Что сделать	Кто выполняет	Точность	Что пересчитается в альбоме	Чем подтверждается	Закрывает вопросы реестра
О-8	Кухня-гостиная (пом. 1), Спальня (пом. 2), Ванная (пом. 3), Санузел (пом. 4), Прихожая (пом. 5), Гардеробная (пом. 6)	Обмер	Нивелировка плиты перекрытия и существующего пола после демонтажа покрытий: отметки в углах и по сетке, перепады по помещению, уклоны, отметки порогов (чистый пол в мокрых зонах принят -15 мм, 0 мм). Принятая толщина стяжки 33 мм, 50 мм и отметка чистого пола — расчётные, не от замера плиты.	Архитектор	±5 мм по отметке; ровность просвет под 2-метровой рейкой, горизонталь против 0,2 % длины помещения	Толщина стяжки и отметка чистого пола; уклоны к трапам и пороги; выпуски К1 относительно чистого пола (план разводки); объёмы стяжки и смеси в ВОР и спецификации. Листы: л. 43, 47 — План полов л. 30 — Схема разводки водопровода и канализации	акт контрольного обмера	Вопроса в реестре нет: Альбом принимает отметки плиты и толщину пирога пола без нивелировки. Результат принимает: Отделочник
О-9	Кухня-гостиная (пом. 1), Спальня (пом. 2), Ванная (пом. 3), Санузел (пом. 4), Прихожая (пом. 5), Гардеробная (пом. 6)	Обмер	Вертикаль и плоскостность стен: отклонение от вертикали по высоте стены (отвес или лазерный уровень), просвет под правилом 2 м, кривизна углов. Нужно там, где от стены зависит изделие: облицовка плиткой (пом. 3, 4), штукатурка и окраска (пом. 1, 2, 5, 6), встроенная мебель и кухня (пом. 1, 5).	Архитектор	до 1 мм на 2 м (правило и клиновой щуп); вертикаль — мм на высоту стены, отклонения подписываются на плане	Толщина штукатурки и расход смеси в ВОР и спецификации; раскладка плитки (подрезка у стен); зазоры и крепление встроенной мебели и кухни. Листы: л. 43–46 — Раскладка плитки л. 48 — Ведомость отделки помещений	акт контрольного обмера	Вопроса в реестре нет: Альбом принимает стены ровными и вертикальными без замера. Результат принимает: Отделочник

Документы и данные закупки (не на объекте)

№	У кого, откуда	Способ	Что получить	К какому сроку	Что пересчитается в альбоме	Чем подтверждается	Закрывает вопросы реестра
О-10	адрес объекта, СП 131.13330	Документ	Климатический подрайон по СП 131.13330 (по адресу объекта)	до заказа каркаса потолков	план потолков, разрезы, ведомость объёмов Листы: л. 40 — План потолков	копия документа	К-4 Результат принимает: Архитектор
О-11	заказчик; организация, выдавшая технические условия	Документ	Технические условия на присоединение: разрешённая мощность (принято 15 кВт по типовой квартире).	до утверждения однолинейной схемы щита	однолинейная схема щита: вводной аппарат и группы Листы: л. 24 — Однолинейная схема щита	копия документа	К-6 Результат принимает: Инженер-электрик

Допущения и предложения на листе

Основа листа: размеры сняты с плана заказчика, контрольный обмер не выполнен (К-5); высота потолка 2700 мм принята: на плане заказчика не указана (К-5); подрайон климата не задан — принят не северный (жилые от 2,5 м) (К-4); толщины стен приняты: наружные 250 мм, перегородки 120 мм — не обмерены (К-5); разрешённая мощность 15 кВт принята по типовой квартире, технических условий нет (К-6).

См. лист открытых вопросов (лист 6, записи К-4–К-6).

Изм.	Кол.уч	Лист	№ док.	Подп.	Дата
Разраб.		Кырлан А.С.			04.11.26
Пров.					
ГИП					
Н. контр.					
Утв.					

ГД-2026-006-АИ

Квартира 58 м²

Общая площадь 55,23* м² · * размеры приняты, не замерены (реестр — л. 6, 7, К-5)

Дизайн-проект интерьера	Стадия	Лист	Листов
	РП	9	87

Задание на контрольный обмер и обследование.
Лист 2 из 3
М б/м

Кырлан Александр Сергеевич

выпуск 04.11.2026 № 94e55e632e · стр. 9 из 96

Задание на контрольный обмер и обследование. Лист 3 из 3

ПРЕДВАРИТЕЛЬНО · не для производства работ · открыто пунктов: 10 (реестр — л. 6, 7)

Что замерить, вскрыть и получить до заказа материалов и изделий

Документы и данные закупки (не на объекте) (продолжение)

№	У кого, откуда	Способ	Что получить	К какому сроку	Что пересчитается в альбоме	Чем подтверждается	Закрывает вопросы реестра
О-12	паспорт модели	Документ	Модель стиральной машины: габарит (ширина 600, глубина ≤ 450, высота ≤ 850 под столешницу), тип загрузки, положение подвода и слива	до заказа кухни	ниша М11** кухни, выводы В1/К1, розетка Листы: л. 29 — План выводов сантехники л. 18 — План расстановки мебели л. 24 — Однолинейная схема щита	копия документа	К-7 Результат принимает: Инженер ВК (вода, канализация)
О-13	Поставщик изделий; Спальня (пом. 2)	Закупка	Паспорт или монтажная схема выбранной модели: КВ-2* допустимая длина трассы фреона (минимальная и максимальная), перепад высот между блоками, место наружного блока. Принято в проекте: длина петли принята по типовому минимуму 3 м; паспорта выбранной модели нет.	До закрытия трасс и разводки	Габариты и положение изделий на планах и развёртках, выводы (вода, слив, электро), монтажные зазоры; знак «*» у марки снимается паспортом или чертежом. Листы: л. 18 — План расстановки мебели	паспорт изделия или партии	Вопроса в реестре нет Результат принимает: Инженер ОВ

Примечания

1. Подтверждение: акт контрольного обмера (дата, кто присутствовал, прибор, перечень промеров с результатами, подписи присутствующих); к акту — фото вскрытий и узлов и техническое заключение организации, выполнившей обследование.
2. Номера листов — по ведомости рабочих чертежей комплекта (лист «Общие данные»).
3. Пункт исключается из задания при следующем выпуске, когда акт подписан, значение внесено в проект и листы перевыпущены; знак «*» у величины снимается только замером.

Допущения и предложения на листе

Основа листа: размеры сняты с плана заказчика, контрольный обмер не выполнен (К-5); высота потолка 2700 мм принята: на плане заказчика не указана (К-5); подрайон климата не задан — принят не северный (жилые от 2,5 м) (К-4); толщины стен приняты: наружные 250 мм, перегородки 120 мм — не обмерены (К-5); разрешённая мощность 15 кВт принята по типовой квартире, технических условий нет (К-6).

Знак «*» — принято, не замерено и не подтверждено (замерить на объекте): КВ-2 — длина петли принята по типовому минимуму 3 м; паспорта выбранной модели нет.

Знак «**» — предложение проектировщика, заказчиком не утверждено (согласовать с заказчиком): К-7: М11 — место стиральной машины: вместо модуля с ящиками 400 справа от варочной; ряд до 3420, журнальный стол М21 (с х 3440) не мешает загрузке.

См. лист открытых вопросов (лист 6, записи К-4–К-7).

Изм.	Кол.уч	Лист	№ док.	Подп.	Дата
Разраб.		Кырлан А.С.			04.11.26
Пров.					
ГИП					
Н. контр.					
Утв.					

ГД-2026-006-АИ

Квартира 58 м²

Общая площадь 55,23* м² · * размеры приняты, не замерены (реестр — л. 6, 7, К-5)

Дизайн-проект интерьера

Стадия	Лист	Листов
РП	10	87

Задание на контрольный обмер и обследование.
Лист 3 из 3
М б/м

Кырлан Александр Сергеевич

выпуск 04.11.2026 № 94e55e632e · стр. 10 из 96

График закупок и работ. Лист 1 из 3

ПРЕДВАРИТЕЛЬНО · не для производства работ · открыто пунктов: 10 (реестр — л. 6, 7)

Что заказывать и когда не раньше чего: относительный порядок без дат; срок поставки — из данных или «не задан» с записью реестра

Лист не содержит дат: контрольного обмера, подписанных решений автора и договоров ещё нет, и любая дата была бы выдумана. Вместо календаря — порядок и условия: замер → решение и выбор изделия → заказ → срок поставки → работа, которую позиция блокирует.
Срок поставки печатается как срок, только если он задан в данных позиции. Нет — «срок поставки не задан» и ссылка на вопрос реестра о сроках; типовой диапазон практики стоит рядом как ориентир и заказывать по нему нельзя. Номера З-N и Р-N — строки этого листа, К-N — записи реестра открытых вопросов, О-N — позиции задания на контрольный обмер.

Закупки: что заказывается, от чего зависит заказ и какую работу блокирует

№	Позиция и где	1. Замер до заказа	2. Решение, выбор изделия, паспорт	3. Условие заказа	4. Срок поставки	5. Блокирует работу	Закрывает вопросы реестра
З-1	Двери скрытого монтажа с коробом под покраску в существующих проёмах: Д-2, Д-3, Д-4 — 5 шт. пом. 5, 6	О-7: обмер: все помещения квартиры (К-5); до заказа мебели, дверей и каркаса потолков		После 1 и 2 и после получения срока у поставщика (вопроса о сроках нет); дата заказа — когда срок известен, не позднее чем за срок до начала Р-5.	срок поставки не задан (записи реестра нет) Ориентир практики (не срок поставщика): ≈ 30 дн.	Р-5 «штукатурка»: короб ставят до штукатурки (коробку ставят на черновой стадии; полотно навешивают после чистовой отделки стен)	К-5
З-2	Кухонный гарнитур по проекту кухни: модули М4, М5, М6, М7, М11**, М8, М10 пом. 1			После 1 и 2 и после получения срока у поставщика (вопроса о сроках нет); дата заказа — когда срок известен, не позднее чем за срок до начала Р-15.	срок поставки не задан (записи реестра нет) Ориентир практики (не срок поставщика): 4–8 нед. от замера	Р-15 «кухня и мебель»: замер кухни — по готовым стенам после штукатурки или плитки, до чистового пола; производство идёт параллельно со стяжкой и отделкой	
З-3	Встраиваемая техника кухни: М4 холодильник, М11** washer пом. 1			После 1 и 2 и после получения срока у поставщика (вопроса о сроках нет); дата заказа — когда срок известен, не позднее чем за срок до начала Р-15.	срок поставки не задан (записи реестра нет)	Р-15 «кухня и мебель»: паспорта и монтажные схемы — до изготовления модулей кухни: нишу и вентзазоры задаёт модель, а не типовая схема 60 см	
З-4	Стиральная машина: П6** (вертикальная загрузка 400 × 600 мм — условие закупки) пом. 1		О-12: Модель стиральной машины: габарит (ширина 600, глубина ≤ 450, высота ≤ 850 под столешницу), тип загрузки, положение подвода и слива (К-7); до заказа кухни	После 1 и 2 и после получения срока у поставщика (вопроса о сроках нет); дата заказа — когда срок известен, не позднее чем за срок до начала Р-4.	срок поставки не задан (записи реестра нет)	Р-4 «черновая сантехника»: габарит и подводка — до закрытия люка и разводки	К-7
З-5	Сантехнические приборы и инсталляции: П4, П1**, П3**, П20 пом. 1, 3, 4	О-3: обмер: у окон		После 1 и 2 и после получения срока у поставщика (вопроса о сроках нет); дата заказа — когда срок известен, не позднее чем за срок до начала Р-4.	срок поставки не задан (записи реестра нет)	Р-4 «черновая сантехника»: инсталляцию ставят до обшивки ГКЛВ и до гидроизоляции стены	
З-6	Керамогранит и плитка: 2 поз. по артикулу и формату, 46,11 м² по раскладке пом. 3, 4, 5	О-8: обмер: Кухня-гостиная (пом. 1), Спальня (пом. 2), Ванная (пом. 3), Санузел (пом. 4), Прихожая (пом. 5), Гардеробная (пом. 6) О-9: обмер: Кухня-гостиная (пом. 1), Спальня (пом. 2), Ванная (пом. 3), Санузел (пом. 4), Прихожая (пом. 5), Гардеробная (пом. 6)		После 1 и 2 и после получения срока у поставщика (вопроса о сроках нет); дата заказа — когда срок известен, не позднее чем за срок до начала Р-9.	срок поставки не задан (записи реестра нет)	Р-9 «плитка»: калибр партии измеряют до раскладки, раскладку пересчитывают до заказа	
З-7	Покрытие пола (доска) и плинтус: пом. 1, 2, 6 пом. 1, 2, 6	О-8: обмер: Кухня-гостиная (пом. 1), Спальня (пом. 2), Ванная (пом. 3), Санузел (пом. 4), Прихожая (пом. 5), Гардеробная (пом. 6)		После 1 и 2 и после получения срока у поставщика (вопроса о сроках нет); дата заказа — когда срок известен, не позднее чем за срок до начала Р-12.	срок поставки не задан (записи реестра нет)	Р-12 «чистовые полы»: артикул и партия — до заказа; доску привозят к чистовым полам	
З-8	Встроенная мебель по замеру цеха: М9 пом. 5	О-7: обмер: все помещения квартиры (К-5); до заказа мебели, дверей и каркаса потолков		После 1 и 2 и после получения срока у поставщика (вопроса о сроках нет); дата заказа — когда срок известен, не позднее чем за срок до начала Р-15.	срок поставки не задан (записи реестра нет) Ориентир практики (не срок поставщика): 4–8 нед. от замера	Р-15 «кухня и мебель»: цех замеряет по готовым стенам; производство 4–8 недель идёт параллельно с отделкой	К-5

Допущения и предложения на листе

Основа листа: размеры сняты с плана заказчика, контрольный обмер не выполнен (К-5); высота потолка 2700 мм принята: на плане заказчика не указана (К-5); подрайон климата не задан — принят не северный (жилые от 2,5 м) (К-4); толщины стен приняты: наружные 250 мм, перегородки 120 мм — не обмерены (К-5); разрешённая мощность 15 кВт принята по типовой квартире, технических условий нет (К-6).

Знак «**» — предложение проектировщика, заказчиком не утверждено (согласовать с заказчиком): К-2: П1 — ванна 1500 вместо 1600 — не заходит в проход перед проёмом Д-4; перед ванной 680 мм — глубина помещения; П3 — умывальник у стены В справа от ванны — перед ним свободно 750 мм, до стены Б 90 мм; К-7: М11 — место стиральной машины: вместо модуля с ящиками 400 справа от варочной; ряд до 3420, журнальный стол М21 (с х 3440) не мешает загрузке; П6 — стиральная машина на кухне: в ванной и санузле места нет; подвод ХВС с шаровым краном, слив — встраиваемый сифон с обратным клапаном (водяной затвор), отдельная группа 6 щита с УЗО 30 мА.

См. лист открытых вопросов (лист 6, записи К-2, К-4–К-7).

Изм.	Кол.уч	Лист	№ док.	Подп.	Дата
Разраб.		Кырлан А.С.			04.11.26
Пров.					
ГИП					
Н. контр.					
Утв.					

ГД-2026-006-АИ

Квартира 58 м²

Общая площадь 55,23* м² · * размеры приняты, не замерены (реестр — л. 6, 7, К-5)

Дизайн-проект интерьера

Стадия	Лист	Листов
РП	11	87

График закупок и работ. Лист 1 из 3

М б/м

Кырлан Александр Сергеевич

выпуск 04.11.2026 № 94e55e632e · стр. 11 из 96

График закупок и работ. Лист 2 из 3

ПРЕДВАРИТЕЛЬНО · не для производства работ · открыто пунктов: 10 (реестр — л. 6, 7)

Что заказывать и когда не раньше чего: относительный порядок без дат; срок поставки — из данных или «не задан» с записью реестра

Работы: порядок и что не даёт начать

№	Работа (стадия технологической последовательности)	После	Что должно быть к началу: условия и закупки	Не начинать, пока открыто в реестре
Р-1	Демонтаж покрытий, отделки стен и потолков, дверных блоков и приборов; конструкции, стены и перегородки не трогать до технического заключения (стадия 1)		до начала: запрошены документы на дом и БТИ; контрольный обмер до демонтажа (что видно) сделан	
Р-2	Контрольный обмер на голых стенах и обследование (задание — лист «Задание на контрольный обмер») (стадия 2)	Р-1	после снятия отделки: видны стояки, каналы, щиток, толщины стен; до заказа всего, что делают по размеру	
Р-3	Черновая электрика: штробы, короба, гофра, подрозетники, щит (стадия 4)	Р-2	до начала: план электрики с высотами утверждён; штробы в стенах — только после технического заключения; мебель расставлена	К-6: Разрешённая мощность 15 кВт принята по типовой квартире, технических условий в материалах объекта нет.
Р-4	Черновая сантехника и вентиляция: разводка, выводы, инсталляции, короба стояков (стадия 5)	Р-2	до начала: положение стояков замерено; модели инсталляций и машины выбраны (габариты рамы, подводка); инсталляцию ставят до обшивки ГКЛВ и до гидроизоляции Закупки к началу: З-4 (стиральная машина), З-5 (сантехника)	К-7: Места стиральной машины в квартире не было.
Р-5	Коробки скрытых дверей, затем штукатурка стен и откосов (стадия 6)	Р-2, Р-3, Р-4	до начала: электрика и сантехника смонтированы, штробы заделаны; коробки скрытых дверей установлены до штукатурки (поэтому заказ дверей — раньше работы) Закупки к началу: З-1 (двери скрытого монтажа)	К-5: Основа альбома — план заказчика без контрольного обмера: размеры помещений сняты с плана, высота потолка 2700 мм и толщины стен (наружные 250 мм, перегородки 120 мм) приняты — на плане они не указаны.
Р-6	Стяжка пола и тёплый пол (стадия 7)	Р-5	до начала: штукатурка сделана; трубы под стяжкой приняты; нивелировка плиты выполнена	
Р-7	Гидроизоляция санузлов и тест проливом (стадия 8)	Р-6	до начала: стяжка набрала прочность и сухая по инструкции гидроизоляции; выводы стоят на проектных отметках	
Р-8	ГКЛ: короба инсталляции и стояков, ниши, потолки (стадия 9)	Р-3, Р-4	до начала: черновые сети в зоне коробов приняты; закладные под тяжёлое и карнизы стоят; светильники выбраны (вырезы)	

Допущения и предложения на листе

Основа листа: размеры сняты с плана заказчика, контрольный обмер не выполнен (К-5); высота потолка 2700 мм принята: на плане заказчика не указана (К-5); подрайон климата не задан — принят не северный (жилые от 2,5 м) (К-4); толщины стен приняты: наружные 250 мм, перегородки 120 мм — не обмерены (К-5); разрешённая мощность 15 кВт принята по типовой квартире, технических условий нет (К-6).

См. лист открытых вопросов (лист 6, записи К-4–К-6).

Изм.	Кол.уч	Лист	№ док.	Подп.	Дата
Разраб.		Кырлан А.С.			04.11.26
Пров.					
ГИП					
Н. контр.					
Утв.					

ГД-2026-006-АИ

Квартира 58 м²

Общая площадь 55,23* м² · * размеры приняты, не замерены (реестр — л. 6, 7, К-5)

Дизайн-проект интерьера

Стадия	Лист	Листов
РП	12	87

График закупок и работ. Лист 2 из 3

М б/м

Кырлан Александр Сергеевич

График закупок и работ. Лист 3 из 3

ПРЕДВАРИТЕЛЬНО · не для производства работ · открыто пунктов: 10 (реестр — л. 6, 7)

Что заказывать и когда не раньше чего: относительный порядок без дат; срок поставки — из данных или «не задан» с записью реестра

Работы: порядок и что не даёт начать (продолжение)

№	Работа (стадия технологической последовательности)	После	Что должно быть к началу: условия и закупки	Не начинать, пока открыто в реестре
Р-9	Плитка и керамогранит: стены, затем пол; фартук (стадия 10)	Р-6, Р-7, Р-8	до начала: гидроизоляция принята; плитка выбрана, калибр партии измерен, раскладка пересчитана и подписана Закупки к началу: З-6 (плитка)	
Р-10	Шпаклёвка стен и потолков под окраску (стадия 11)	Р-5, Р-8, Р-9	до начала: плитка готова (грязные работы закончены); штукатурка и ГКЛ сухие	
Р-11	Окраска стен, потолков, откосов (стадия 13)	Р-10	до начала: шпаклёвка отшлифована и огрунтована; выкрасы утверждены, колеровка одной партией	
Р-12	Чистовые полы: инженерная доска (стадия 14)	Р-9, Р-11	до начала: влажность основания в норме, мокрые работы закончены; доска выбрана и привезена Закупки к началу: З-7 (доска и плинтус)	
Р-13	Полотна межкомнатных дверей, плинтусы, пороги (стадия 15)	Р-11, Р-12	до начала: чистовой пол уложен; полотна скрытых дверей — после чистовой отделки стен	
Р-14	Чистовая электрика и сантехника: механизмы, светильники, смесители, приборы (стадия 16)	Р-11, Р-13	до начала: отделка готова; механизмы, светильники и приборы выбраны и привезены	
Р-15	Кухня, встроенная и корпусная мебель, бытовая техника (стадия 17)	Р-13, Р-14	до начала: чистовая сантехника и электрика подведены к местам мебели; замер кухни снят по готовым стенам (после штукатурки или плитки, до чистового пола) Закупки к началу: З-2 (кухонный гарнитур), З-3 (техника кухни), З-8 (мебель по замеру)	К-5: Основа альбома — план заказчика без контрольного обмера: размеры помещений сняты с плана, высота потолка 2700 мм и толщины стен (наружные 250 мм, перегородки 120 мм) приняты — на плане они не указаны.
Р-16	Сдача: осмотр по чек-листу, дефектная ведомость, устранение замечаний (стадия 18)	Р-14, Р-15	до начала: всё смонтировано; акты скрытых работ подписаны	

Примечания

1. Порядок работ — стадии технологической последовательности из 16 позиций, присутствующих в этом проекте (по строкам ведомости объёмов); остальные стадии таблицы knowledge/remont-tehnologiya.md в проекте не встречаются. Длительности работ не печатаются: их нет ни в данных, ни в нормах для этого объекта.
2. Типовые сроки — ориентир практики, не срок поставщика: скрытые двери — короб около 10 дн., полотно под покраску до 3 нед., шпон 4–5 нед., в среднем около 30 дн. (knowledge/workers/foreman.md, п. 2.4 (profil-doors)); кухня и корпусная мебель — 4–8 недель от замера (knowledge/remont-tehnologiya.md, разд. 2; knowledge/workers/foreman.md, п. 2.4). Заказ по ориентиру не назначается: срок получают у поставщика (вопрос реестра), после чего заказ планируют «не позднее чем за срок до начала работы».
3. Условия заказа берутся из реестра открытых вопросов и задания на контрольный обмер: позиция заказывается, когда закрыты замер (графа 1) и решение (графа 2). Закрывать их может только факт или решение автора с подписью; снять строку с листа можно только закрыв запись реестра.
4. Заказ по размеру до контрольного обмера не делают: двери, кухня и встроенная мебель зависят от обмера (К-11, К-13); скрытые двери, кроме того, зависят от решения по нише санузла 2 (проём Д-5 в перегородке П-1).
5. Номера листов — по ведомости рабочих чертежей комплекта (лист «Общие данные»).

Допущения и предложения на листе

Основа листа: размеры сняты с плана заказчика, контрольный обмер не выполнен (К-5); высота потолка 2700 мм принята: на плане заказчика не указана (К-5); подрайон климата не задан — принят не северный (жилые от 2,5 м) (К-4); толщины стен приняты: наружные 250 мм, перегородки 120 мм — не обмерены (К-5); разрешённая мощность 15 кВт принята по типовой квартире, технических условий нет (К-6).

См. лист открытых вопросов (лист 6, записи К-4–К-6).

Изм.	Кол.уч	Лист	№ док.	Подп.	Дата
Разраб.		Кырлан А.С.			04.11.26
Пров.					
ГИП					
Н. контр.					
Утв.					

ГД-2026-006-АИ

Квартира 58 м²

Общая площадь 55,23* м² · * размеры приняты, не замерены (реестр — л. 6, 7, К-5)

Дизайн-проект интерьера

Стадия	Лист	Листов
РП	13	87

График закупок и работ. Лист 3 из 3

М б/м

Кырлан Александр Сергеевич

выпуск 04.11.2026 № 94e55e632e · стр. 13 из 96

01

Архитектурные решения


Кырлан Александр Сергеевич

выпуск 04.11.2026 · 94e55e632e · стр. 14 из 96

Обмерный план

Существующее положение · размеры в мм · отметки от чистого пола

ПРЕДВАРИТЕЛЬНО · не для производства работ · открыто пунктов: 10 (реестр — л. 6, 7)

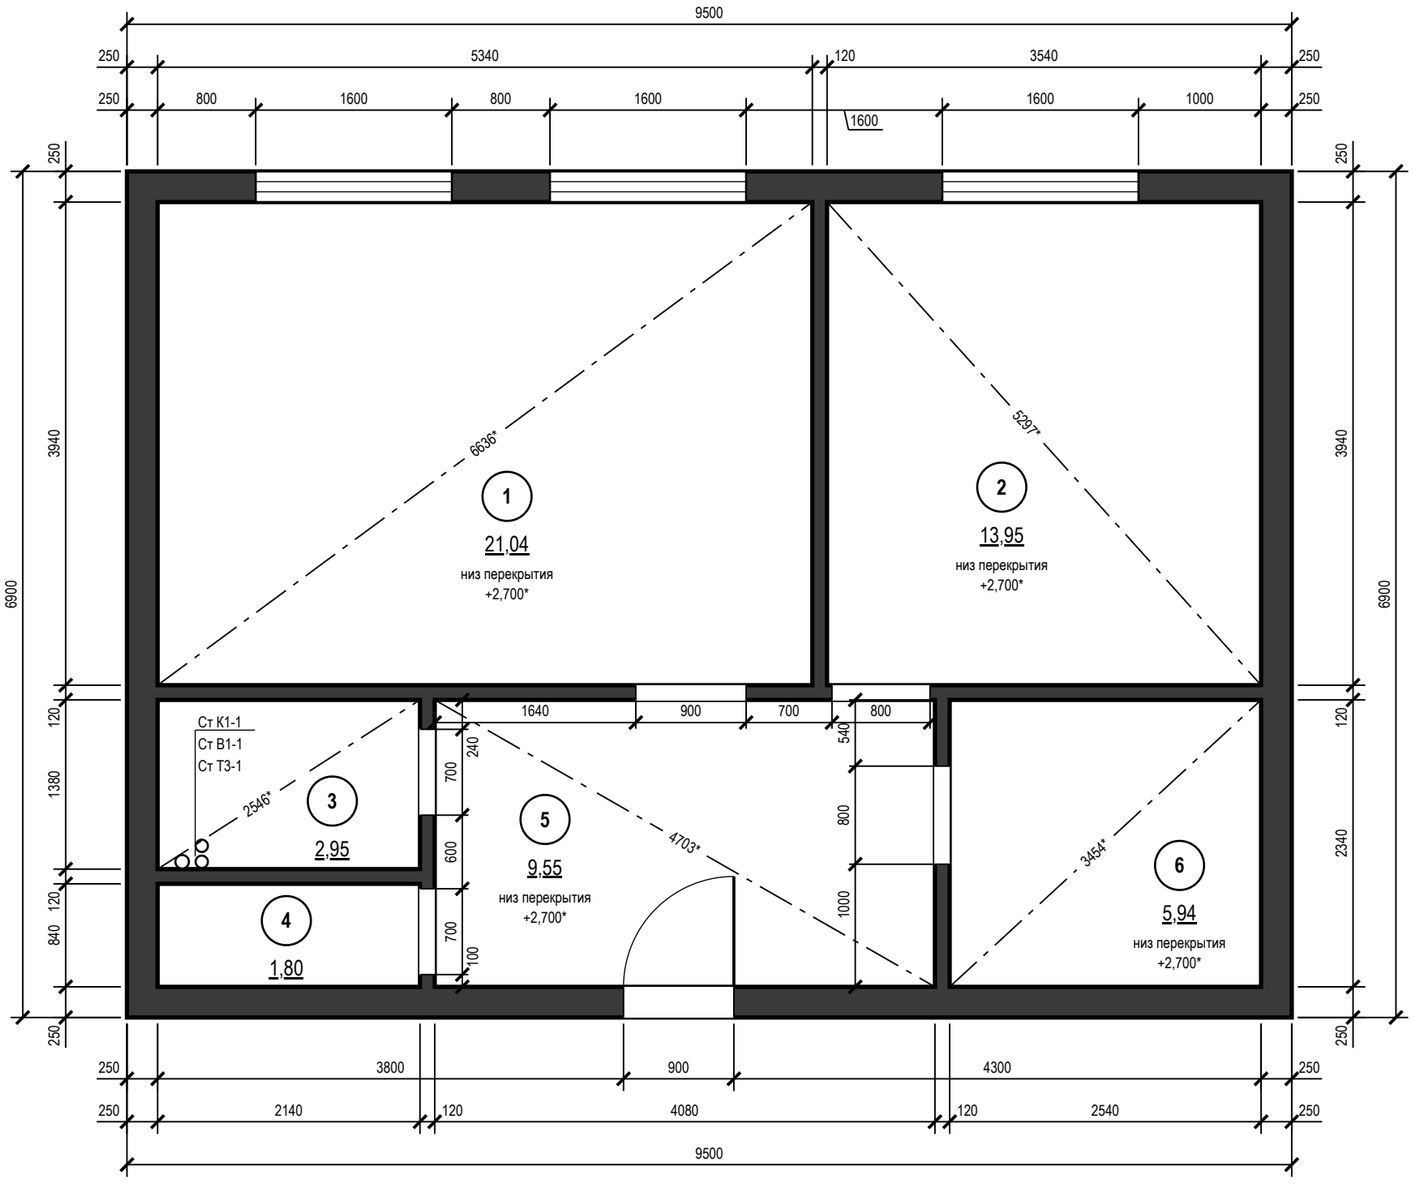

Экспликация помещений

№	Наименование	Площадь, м²
1	Кухня-гостиная	21,04
2	Спальня	13,95
3	Ванная	2,95
4	Санузел	1,80
5	Прихожая	9,55
6	Гардеробная	5,94
	Итого (общая площадь)	**55,23**

Условные обозначения

- существующие стены (сечение)
- окно (рама, остекление)
- проём существующий, без заполнения (откосы)
- стояк: К1 — канализация, В1 — ХВС, Т3 — ГВС
- диагональ помещения — контроль прямоугольности
- (1) номер помещения, площадь м²

Примечания

1. Размеры — в мм по чистым поверхностям стен до отделки (по плану заказчика); площади — в м² по тем же размерам. До начала работ выполнить контрольный обмер.
2. За отметку ±0,000 принят чистый пол, не существующий (блок отметок). «Низ перекрытия» у марки помещения — отметка низа перекрытия от ±0,000, как на развёртках и плане потолков (не высота потолка: потолок — по плану потолков); отметка со знаком «*» — принятая, не замер (вопрос К-5).
3. Толщины стен: наружные 250 мм, перегородки 120 мм; отличающиеся толщины и уступы размерами на плане.
4. Несущие стены не определены: до технического заключения все стены считать несущими; проёмы и штробы в них не выполнять.
5. Дверные проёмы показаны без заполнения (двери — лист 16); высота дверных проёмов 2100 мм; низ окон (подоконник) 800 мм от чистого пола, высота окон 1600 мм.
6. Диагонали — контрольные размеры; «*» — расчёт по принятому контуру (К-5), при обмере заменить замеренным; расхождение более 5 мм подписать на плане как перекос.
7. Размеры проверить на месте до начала работ; расхождение контрольных промеров ≤ 2 %.
8. Размеры короче 1 мм на листе цепочкой не показаны (две выносные линии на таком расстоянии сливаются): пом. 5, стена А — 40 мм от проёма до угла.

Отметки по высоте

±0,000	чистый пол пом. 1, 2, 5, 6; отсчёт высот
−0,015	чистый пол пом. 3, 4, ниже на 15 мм
−0,064*	верх плиты — расчёт, не замер (задание на обмер)
сущ. пол	снимается до плиты; не замерен (задание на обмер)

Допущения и предложения на листе

Основа листа: размеры сняты с плана заказчика, контрольный обмер не выполнен (К-5); высота потолка 2700 мм принята: на плане заказчика не указана (К-5); подрайон климата не задан — принят не северный (жилые от 2,5 м) (К-4); толщины стен приняты: наружные 250 мм, перегородки 120 мм — не обмерены (К-5); разрешённая мощность 15 кВт принята по типовой квартире, технических условий нет (К-6).

Открытые вопросы и конфликты по листу: К-5.

См. лист открытых вопросов (лист 6, записи К-4–К-6).

1000 мм · печать 1:1

Изм.	Кол.уч	Лист	№ док.	Подп.	Дата
Разраб.		Кырлан А.С.			04.11.26
Пров.					
ГИП					
Н. контр.					
Утв.					

ГД-2026-006-АИ

Квартира 58 м²

Общая площадь 55,23* м² · * размеры приняты, не замерены (реестр — л. 6, 7, К-5)

Дизайн-проект интерьера

Стадия	Лист	Листов
РП	14	87

Обмерный план

М 1:50


Кырлан Александр Сергеевич

выпуск 04.11.2026 № 94e55e632e · стр. 15 из 96

План демонтажа и монтажа перегородок

Перепланировка не выполняется · существующие стены сохраняются · размеры в мм


ПРЕДВАРИТЕЛЬНО · не для производства работ · открыто пунктов: 10 (реестр — л. 6, 7)

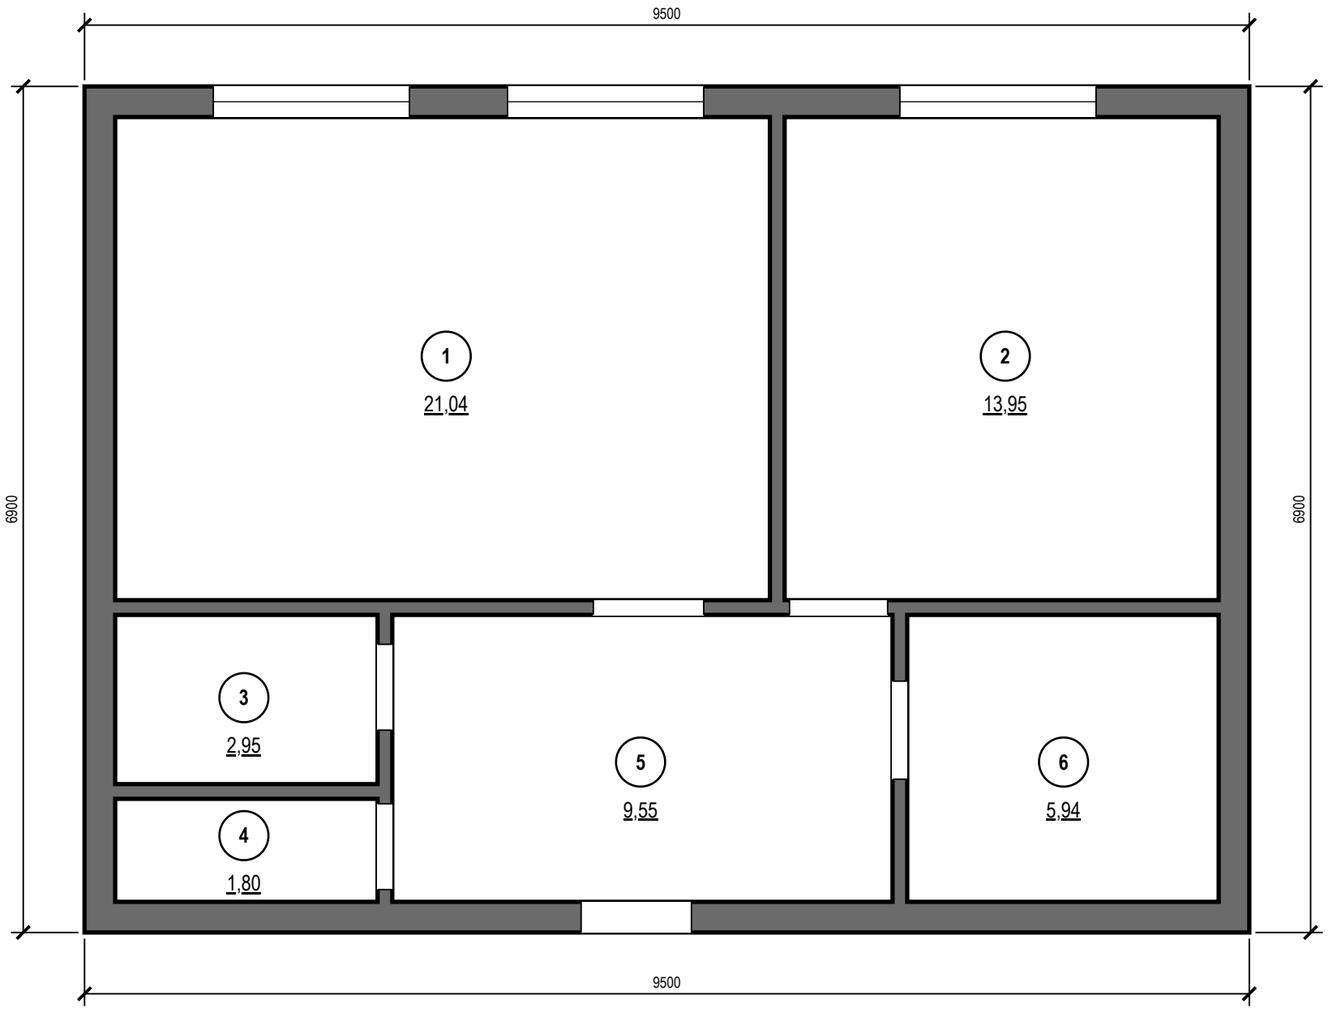

Условные обозначения

- существующие стены — сохраняются; несущие не определены — считать несущими
- демонтируемые конструкции — на плане нет
- возводимые перегородки — на плане нет
- проём существующий, без заполнения (откосы)
- (1) номер помещения, площадь м²

Отметки по высоте

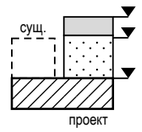

±0,000	чистый пол пом. 1, 2, 5, 6; отсчёт высот
−0,015	чистый пол пом. 3, 4, ниже на 15 мм
−0,064*	верх плиты — расчёт, не замер (задание на обмер)
сущ. пол	снимается до плиты; не замерен (задание на обмер)

Примечания

1. Перепланировка не выполняется: несущие и ненесущие стены, перегородки и плиты перекрытия не демонтируются, новые стены не возводятся; существующие стены и перегородки сохраняются.
2. Дверные блоки — по плану дверей (лист 16); существующие проёмы не расширяются.
3. Демонтаж существующих покрытий пола, стен и потолка, дверных блоков и сантехприборов (если есть) — до основания; объёмы демонтажа — для справки, по факту на объекте.
4. За отметку ±0,000 принят чистый пол, не существующий (блок отметок). Размеры — в мм по чистовой поверхности стен до отделки.
5. Размеры проверить на месте до начала работ: расхождение с обмером — не более 2 % (иначе — к архитектору).
6. Несущие стены не определены: до технического заключения все стены считать несущими — проёмы, ниши и штробы в них не выполнять.

Допущения и предложения на листе

Основа листа: размеры сняты с плана заказчика, контрольный обмер не выполнен (К-5); высота потолка 2700 мм принята: на плане заказчика не указана (К-5); подрайон климата не задан — принят не северный (жилые от 2,5 м) (К-4); толщины стен приняты: наружные 250 мм, перегородки 120 мм — не обмерены (К-5); разрешённая мощность 15 кВт принята по типовой квартире, технических условий нет (К-6).

См. лист открытых вопросов (лист 6, записи К-4–К-6).

1000 мм · печать 1:1

Изм.	Кол.уч	Лист	№ док.	Подп.	Дата
Разраб.		Кырлан А.С.			04.11.26
Пров.					
ГИП					
Н. контр.					
Утв.					

ГД-2026-006-АИ

Квартира 58 м²

Общая площадь 55,23* м² · * размеры приняты, не замерены (реестр — л. 6, 7, К-5)

Дизайн-проект интерьера

Стадия	Лист	Листов
РП	15	87

План демонтажа и монтажа перегородок

М 1:50

Кырлан Александр Сергеевич

выпуск 04.11.2026 № 94e55e632e · стр. 16 из 96

План дверей и ведомость заполнения проёмов


Проёмы, марки заполнения, привязки · размеры в мм

Условные обозначения

- стены (подложка обмера)
- дверь распашная, дуга открывания
- дверь скрытого монтажа
- дверь входная (полотно толще)
- оконный блок
- Д — марка типа (Д-N, ОК-N)
- 1 — номер помещения, площадь м²

Примечания

1. Размеры проёмов и привязки — в миллиметрах от чистых граней стен до отделки; привязка — от угла того помещения, со стороны которого стоит размер. Размер проёма — ширина × высота от чистого пола 0,000. Размеры на плане — проёмов, не полотен: полотно — в ведомости, коробка — по системе. Откос от угла помещения до проёма с коробкой — не менее 50 мм.
2. Марки в кружках — типы заполнения проёмов (ГОСТ 21.501-2018, п. 5.3.2); одна марка — один типоразмер; количество сверено с планом.
3. Открывание: Л — петли слева, П — справа, если смотреть со стороны, куда открывается полотно (на себя).
4. Скрытые двери (Д-2…Д-4): проём замерить в чистоте; блок заказать до штукатурки (≈ 30 дн.), короб ставить до штукатурки; полотно навесить после чистовой отделки, красить в цвет стен. Порядок практика монтажа, изготовитель подтверждает.
5. Д-2…Д-4 — существующие проёмы, до техзаключения не расширять (К-3).
6. Полотно «расч.» — по проёму с запасом по каталогам, заказ — по таблице проёмов модели; Д-2…Д-4: проём 2100, а под полотно 2000 по каталогам нужен 2050–2080, под 2100 — 2150–2180: высоту проёма по модели; Д-1: входной блок по ГОСТ 31173-2016 — задать при выборе блока.
7. Экспликация помещений — лист 14; в марках помещений — номер и площадь, м².
8. Привязка проёма к углу помещения меньше 1 мм на листе, размер на плане не показан: Д-3 — 40 мм; Д-4 — 40 мм.

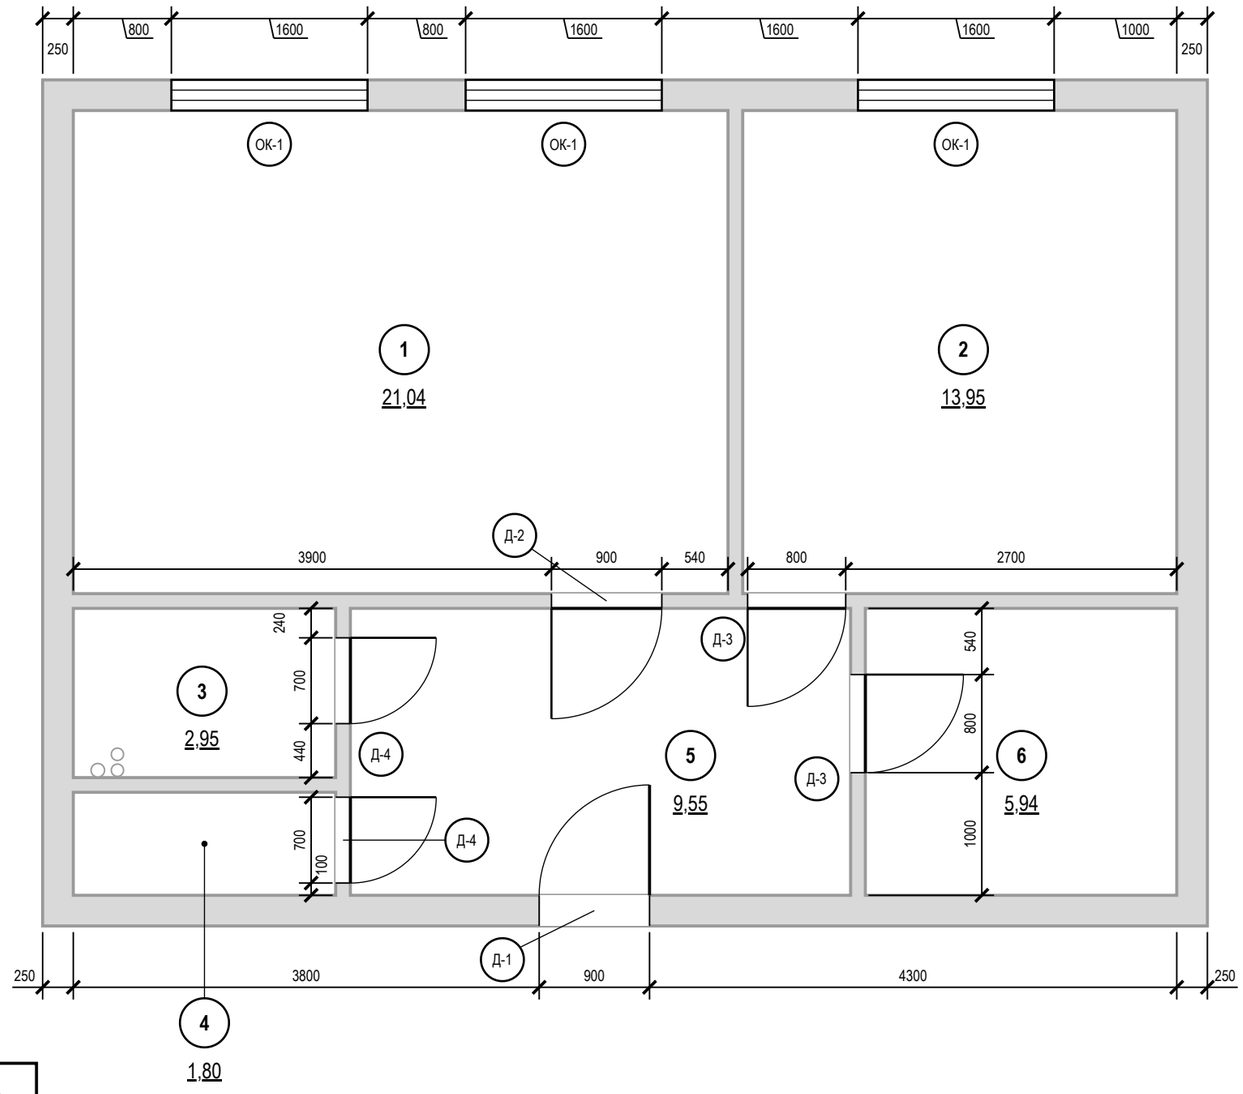

Ведомость заполнения проёмов

Марка	Наименование, обозначение	Проём ш×в, мм	Полотно (расч.)	Кол.	Откр.	Отделка полотна	Фурнитура	Прим.
Д-1	Блок дверной входной, ГОСТ 31173-2016	900×2100	блок задать	1	Л	в комплекте блока	в комплекте блока (замки, глазок)	
Д-2	Дверь скрытого монтажа, Софья (SOFIA) Скрытые двери	900×2100	800×2000	1	Л	S 1502-Y50R — пом. 5, S 1002-Y50R — пом. 1	скрытые петли 3D, магнитный замок	
Д-3	Дверь скрытого монтажа, Софья (SOFIA) Скрытые двери	800×2100	700×2000	2	Л, П	окраска S 1502-Y50R с двух сторон; V503 пом. 6, S 1502-Y50R пом. 5	скрытые петли 3D, магнитный замок	
Д-4	Дверь скрытого монтажа, Софья (SOFIA) Скрытые двери	700×2100	600×2000	2	П, П	S 1502-Y50R — пом. 5, в тон облицовки — пом. 3; S 1502-Y50R — пом. 5, в тон облицовки пом. 4	скрытые петли 3D, магнитный замок, фиксатор WC	порог 15
ОК-1	Блок оконный, ГОСТ 23166-2021	1600×1600		3				низ 800

Допущения и предложения на листе

Основа листа: размеры сняты с плана заказчика, контрольный обмер не выполнен (К-5); высота потолка 2700 мм принята: на плане заказчика не указана (К-5); подрайон климата не задан — принят не северный (жилые от 2,5 м) (К-4); толщины стен приняты: наружные 250 мм, перегородки 120 мм — не обмерены (К-5); разрешённая мощность 15 кВт принята по типовой квартире, технических условий нет (К-6).

Открытые вопросы и конфликты по листу: К-3.

См. лист открытых вопросов (лист 6, записи К-3–К-6).

Изм.	Кол.уч	Лист	№ док.	Подп.	Дата
Разраб.		Кырлан А.С.			04.11.26
Пров.					
ГИП					
Н. контр.					
Утв.					

ГД-2026-006-АИ

Квартира 58 м²

Общая площадь 55,23* м² · * размеры приняты, не замерены (реестр — л. 6, 7, К-5)

Дизайн-проект интерьера

Стадия	Лист	Листов
РП	16	87

План дверей и ведомость заполнения проёмов

М 1:50

Кырлан Александр Сергеевич

1000 мм · печать 1:1

выпуск 04.11.2026 № 94e55e632e · стр. 17 из 96

02

Планировочное решение

Кырлан Александр Сергеевич

выпуск 04.11.2026 · 94e55e632e · стр. 18 из 96


Концепция интерьера

Скандинавский · схема нейтральная · 60/30/10 · материалы, образы и зонирование

Идея

Стиль — скандинавский: светло, спокойно, уютно (hygge), естественно, функционально, в меру (lagom). Палитра выведена из выкрасов (колерная карта): база — тёплые нейтрали NCS S 1502-Y50R / S 1002-Y50R на стенах, NCS S 0300-N на потолках; второй цвет — Tikkurila V503 (гардеробная); акцент — пыльный синий NCS S 4010-R90B в текстиле по концепции стиля (текстиль в данных ещё не задан). Цветовая схема — нейтральная, пропорция 60/30/10: база на стенах и потолках, вторичный цвет — в текстиле и мягкой мебели, акцент — точечно.

Мудборд: материалы и фактуры

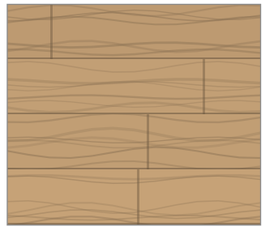

Инженерная доска, дуб натуральный
пол



SG651622R
пол



NCS S 0300-N
потолок, плинтус



NCS S 1502-Y50R
стены



NCS S 1002-Y50R
стены



Winter · Tikkurila V503
стены, потолок, плинтус



610015000370
стены

Палитра 60/30/10

	60 %		30 %	10 %

60 % база — NCS S 1502-Y50R, LRV 72; NCS S 1002-Y50R, LRV 82; NCS S 0300-N, LRV 92

30 % вторичный — Tikkurila V503 Winter, LRV 86

10 % акцент — NCS S 4010-R90B, LRV 27

Функциональное зонирование (М 1:100)



дневная зона: гостиная, кухня, столовая

мокрая зона: санузлы

вход и коммуникации

номер помещения (лист 18)

ночная зона: спальни

хранение: гардеробная, кладовая

функциональная зона в помещении

Образы помещений

1. Кухня-гостиная 21,04 м²

стены NCS S 1002-Y50R
пол — доска, дуб натуральный
свет 3000 K

2. Спальня 13,95 м²

стены NCS S 1502-Y50R
пол — доска, дуб натуральный
свет 2700 K

5. Прихожая 9,55 м²

стены NCS S 1502-Y50R
пол — SG651622R
свет 3000 K

6. Гардеробная 5,94 м²

стены Tikkurila V503
пол — доска, дуб натуральный
свет 3000 K

3. Ванная 2,95 м²

стены Italon 610015000370
пол — SG651622R
свет 3000 K

4. Санузел 1,80 м²

стены Italon 610015000370
пол — SG651622R
свет 3000 K

Материалы и отделка

Инженерная доска, дуб натуральный
масло, 1-полосная, 14/4 мм
пол — пом. 1, 2, 6

SG651622R
пол — пом. 3, 4, 5

610015000370
стены — пом. 3, 4

NCS S 1002-Y50R, LRV 82
стены — пом. 1

NCS S 0300-N, LRV 92
глубокоматовая
потолок, плинтус — пом. 1, 2, 3, 4, 5

NCS S 1502-Y50R, LRV 72
глубокоматовая
стены — пом. 2, 5

Tikkurila V503 Winter, LRV 86
Tikkurila Harmony, матовая
стены, потолок, плинтус — пом. 6

Чего избегаем

1) Холодный белый + серый ламинат + серый диван без дерева
2) Принты олени/Hygge, надписи, лишние подушки
3) Глянцевый лак на дереве, венге, под орех
4) Одна люстра на комнату, свет 4000–6500 K, споты сеткой
5) Тяжёлые шторы с ламбрекенами, лепнина, многоуровневые потолки
6) Три разных светлых дуба в одном помещении

Допущения и предложения на листе

Основа листа: размеры сняты с плана заказчика, контрольный обмер не выполнен (К-5); высота потолка 2700 мм принята: на плане заказчика не указана (К-5); подрайон климата не задан — принят не северный (жилые от 2,5 м) (К-4); толщины стен приняты: наружные 250 мм, перегородки 120 мм — не обмерены (К-5); разрешённая мощность 15 кВт принята по типовой квартире, технических условий нет (К-6).

См. лист открытых вопросов (лист 6, записи К-4–К-6).

Примечания

1. Коды цвета — по веерам производителей (колерная карта, лист 49); перед закупкой краски — выкрас на стене объекта под дневным светом и лампами проекта.
2. Материалы — по ведомости отделки (лист 48); мебель, текстиль и декор — по спецификации (лист 19). Образцы доски, керамогранита и тканей утвердить до заказа.
3. Фактуры на листе условные, цвет передан по HEX-значениям производителей: при печати возможны отклонения, решение — только по физическому образцу.

Изм.	Кол.уч	Лист	№ док.	Подп.	Дата
Разраб.		Кырлан А.С.			04.11.26
Пров.					
ГИП					
Н. контр.					
Утв.					

ГД-2026-006-АИ

Квартира 58 м²

Общая площадь 55,23* м² · * размеры приняты, не замерены (реестр — л. 6, 7, К-5)

Дизайн-проект интерьера

Стадия	Лист	Листов
РП	17	87

Концепция интерьера


М б/м

Кырлан Александр Сергеевич

выпуск 04.11.2026 № 94e55e632e · стр. 19 из 96

План расстановки мебели

Мебель и оборудование · размеры в мм от чистовых стен · марки — по ведомости

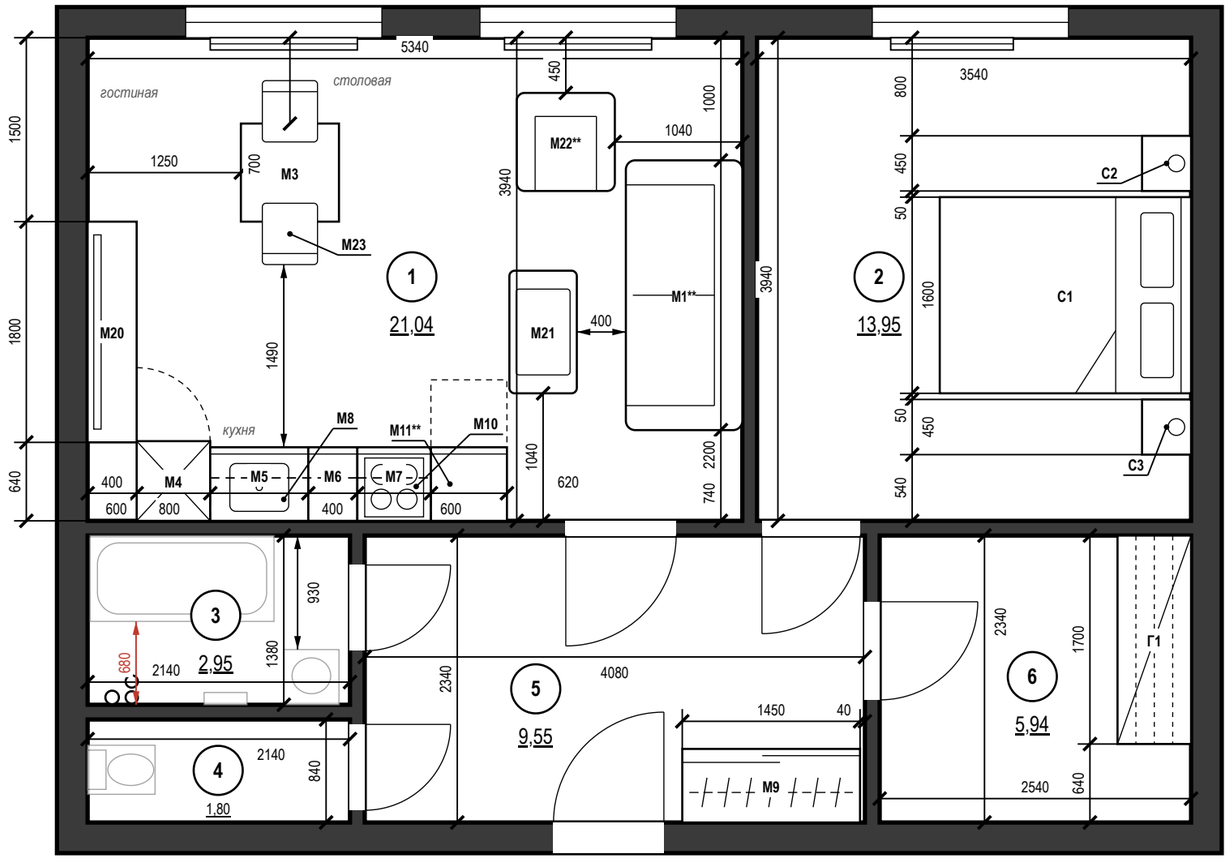

Экспликация помещений

лист 14 · на плане — номера в марках

Ведомость мебели и оборудования

Марка	Наименование	Ш×Г×В, мм	Пом.	Кол.
М4	Пенал кухонный	600×650×2100	1	1
М5	Модуль нижний	800×600×900	1	1
М6	Модуль нижний	400×600×900	1	1
М7	Модуль нижний	600×600×900	1	1
М11**	Ниша под стиральную машину	620×600×900	1	1
М8	Модуль навесной	1200×350×720	1	1
М10	Навесной модуль над варочной	600×350×620	1	1
М1**	Диван	2200×950×850	1	1
М3	Стол обеденный	800×800×750	1	1
М20	ТВ-тумба подвесная с экраном	1800×400×450	1	1
М21	Стол журнальный	550×1000×400	1	1
М22**	Кресло	800×800×800	1	1
С1	Кровать двуспальная	1600×2050×450	2	1
С2	Тумба прикроватная	450×400×500	2	1
С3	Тумба прикроватная	450×400×500	2	1
М9	Шкаф-купе	1450×600×2450	5	1
Г1	Система хранения	1700×600×2400	6	1
М23	Стул обеденный к столу М3	450×500×820	1	2

Ш — вдоль стены (изголовья), Г — от стены (длина кровати)

Материалы, модели, допуск замены — лист 19

Условные обозначения

- мебель и оборудование — габарит в масштабе
- навесные шкафы (низ выше 0,9 м) — невидимый контур
- зона открывания дверец шкафов и техники
- К1 — марка предмета по ведомости мебели
- привязка от чистовой стены, мм
- ширина прохода, зазор, мм
- проход меньше нормы — расстановку изменить
- сантехприборы — подложка (лист ВК)
- радиатор отопления (лист ОВ)
- существующие стены (сечение)
- стояк: К1 — канализация, В1 — ХВС, Т3 — ГВС
- 1 — номер помещения, площадь м²
- *зона* — функциональная зона помещения

Примечания

1. Размеры — в мм от чистовых поверхностей стен, размеры помещений — в свету, привязки — от стен, углов помещения и соседних предметов, проходы и зазоры — стрелками; розетки и выводы под мебель — лист 20, выключатели — лист 22, сантехприборы — лист 29.
2. Общие указания к расстановке (чистовой слой, контрольный обмер, зазоры встроенной мебели, замена покупной) — примечания к спецификации, лист 19.
3. Стулья обеденной группы (М23 — 2 шт.) показаны в рабочем положении, задвинутыми под столешницу на 150 мм.

Допущения и предложения на листе

Основа листа: размеры сняты с плана заказчика, контрольный обмер не выполнен (К-5); высота потолка 2700 мм принята: на плане заказчика не указана (К-5); подрайон климата не задан — принят не северный (жилые от 2,5 м) (К-4); толщины стен приняты: наружные 250 мм, перегородки 120 мм — не обмерены (К-5); разрешённая мощность 15 кВт принята по типовой квартире, технических условий нет (К-6).

Знак «**» — предложение проектировщика, заказчиком не утверждено (согласовать с заказчиком): ИЗ-2: М1 — Было offset 1300…3500: торец дивана в 500 мм от стены В, правые 350 мм проёма Д-2 (3900…4800) упирались в диван; М22 — Было х 4250 — место занял диван М1 (х 4450…5400 от у 1000); К-7: М11 — место стиральной машины: вместо модуля с ящиками 400 справа от варочной; ряд до 3420, журнальный стол М21 (с х 3440) не мешает загрузке.

Открытые вопросы и конфликты по листу: К-2, К-7.

Изменения по листу без подписи: ИЗ-2.

См. лист открытых вопросов (лист 6, записи К-2, К-4–К-7; лист 7, запись ИЗ-2).

1000 мм · печать 1:1

Изм.	Кол.уч	Лист	№ док.	Подп.	Дата
Разраб.		Кырлан А.С.			04.11.26
Пров.					
ГИП					
Н. контр.					
Утв.					

ГД-2026-006-АИ

Квартира 58 м²

Общая площадь 55,23* м² · * размеры приняты, не замерены (реестр — л. 6, 7, К-5)

Дизайн-проект интерьера

Стадия	Лист	Листов
РП	18	87

План расстановки мебели

М 1:50

Кырлан Александр Сергеевич

выпуск 04.11.2026 № 94e55e632e · стр. 20 из 96

Спецификация мебели и оборудования

ПРЕДВАРИТЕЛЬНО · не для производства работ · открыто пунктов: 10 (реестр — л. 6, 7)

Форма 1 ГОСТ 21.110-2013 · позиции мебели — по плану расстановки

Поз.	Наименование и техническая характеристика	Тип, марка, обозначение документа, опросного листа	Код продукции	Поставщик	Ед. измерения	Кол.	Масса 1 ед., кг	Примечание
	Мебель встроенная и корпусная (изготовление по чертежам мебельщика)							
М4	Пенал кухонный, холодильник; корпус ЛДСП 16 мм; фасады — без фасада (прибор отдельностоящий); Ш×Г×В 600×650×2100 мм			изготовление на заказ	шт.	1		пом. 1
М5	Модуль нижний, мойка; корпус ЛДСП 16 мм; фасады — МДФ эмаль 18 мм; Ш×Г×В 800×600×900 мм			изготовление на заказ	шт.	1		пом. 1
М6	Модуль нижний; корпус ЛДСП 16 мм; фасады — МДФ эмаль 18 мм; Ш×Г×В 400×600×900 мм			изготовление на заказ	шт.	1		пом. 1
М7	Модуль нижний, варочная; корпус ЛДСП 16 мм; фасады — МДФ эмаль 18 мм; Ш×Г×В 600×600×900 мм			изготовление на заказ	шт.	1		пом. 1
М8	Модуль навесной; корпус ЛДСП 16 мм; фасады — МДФ эмаль 18 мм; Ш×Г×В 1200×350×720 мм			изготовление на заказ	шт.	1		пом. 1
М10	Навесной модуль над варочной, вытяжка встраивается в дно; корпус ЛДСП 16 мм; фасады — МДФ эмаль 18 мм; Ш×Г×В 600×350×620 мм			изготовление на заказ	шт.	1		пом. 1
М11**	Модуль под встраиваемую ПММ 60; без корпуса (ниша между соседними модулями); фасад на дверь машины — МДФ эмаль 18 мм; цоколь; Ш×Г×В 620×600×900 мм			изготовление на заказ	шт.	1		пом. 1
М9	Шкаф-купе; корпус ЛДСП 16 мм; фасады — ЛДСП 10 мм в алюминиевом профиле; Ш×Г×В 1450×600×2450 мм			изготовление на заказ	шт.	1		пом. 5
Г1	Система хранения: штанги, полки, ящики; каркас и полки — ЛДСП 16 мм, декор «дуб натуральный»; без фасадов; Ш×Г×В 1700×600×2400 мм			изготовление на заказ	шт.	1		пом. 6; крепление к стене
	Мебель покупная							
М1**	Диван; обивка — ткань, цвет Tikkurila V503; Ш×Г×В 2200×950×850 мм			аналог по характеристикам	шт.	1		пом. 1; замена ≤ габарита
М3	Стол обеденный; шпон, дуб натуральный, матовое масло; Ш×Г×В 800×800×750 мм			аналог по характеристикам	шт.	1		пом. 1; замена ≤ габарита
М20	ТВ-тумба подвесная с экраном; шпон, дуб натуральный, матовое масло; Ш×Г×В 1800×400×450 мм			аналог по характеристикам	шт.	1		пом. 1; замена ≤ габарита
М21	Стол журнальный; шпон, дуб натуральный, матовое масло; Ш×Г×В 550×1000×400 мм			аналог по характеристикам	шт.	1		пом. 1; замена ≤ габарита
М22**	Кресло; обивка — ткань, цвет Tikkurila V503; Ш×Г×В 800×800×800 мм			аналог по характеристикам	шт.	1		пом. 1; замена ≤ габарита
М23	Стул обеденный к столу М3; обивка — ткань, цвет Tikkurila V503; каркас — дуб натуральный; Ш×Г×В 450×500×820 мм			аналог по характеристикам	шт.	2		пом. 1; замена ≤ габарита
С1	Кровать двуспальная; мягкое изголовье, обивка — ткань, цвет Tikkurila V503; Ш×Г×В 1600×2050×450 мм			аналог по характеристикам	шт.	1		пом. 2; замена ≤ габарита
С2, С3	Тумба прикроватная; шпон, дуб натуральный, матовое масло; Ш×Г×В 450×400×500 мм			аналог по характеристикам	шт.	2		пом. 2; замена ≤ габарита
	Техника встраиваемая и бытовая (покупные изделия), светильники под розетки							
	Холодильник, в модуле М4	аналог по характеристикам: отдельностоящий, габарит — по проёму		по выбору заказчика до изготовления мебели	шт.	1		пом. 1; по схеме изготовителя
	Варочная панель встраиваемая, индукционная, в модуле М7	аналог по характеристикам: индукционная 60 см, вырез 560 × 490 мм по шаблону модели		по выбору заказчика до изготовления мебели	шт.	1		пом. 1; по схеме изготовителя
	Стиральная машина, в модуле М11**	аналог по характеристикам: тип загрузки — по листу ВК, по листу ВК		по выбору заказчика до изготовления мебели	шт.	1		пом. 1; по схеме изготовителя
	Вытяжка встраиваемая, в модуле М10	аналог по характеристикам: производительность — по расчёту ОВ, шум ≤ 55 дБ(А)		по выбору заказчика до изготовления мебели	шт.	1		пом. 1; по схеме изготовителя
	Торшер, у поз. М3; абажур — ткань или опаловое стекло; лампа 3000 К			аналог по характеристикам	шт.	1		пом. 1; розетка — по плану розеток (ЭОМ)

Примечания

1. Позиции мебели совпадают с марками на плане расстановки (лист 18); размеры Ш×Г×В — Ш вдоль стены, Г от стены.
2. Размеры и привязки плана расстановки — в мм от чистовых поверхностей стен: слой штукатурки 20 мм по блоку и 5 мм шпаклёвки по ГКЛ учтён; привязки — от стен и углов помещения, а не от другой мебели.
3. План расстановки не является документацией для изготовления мебели. Встроенная и корпусная мебель изготавливается по чертежам мебельщика после контрольного обмера (после штукатурки); «стена в стену» — с зазором 10 мм с каждой стороны или с компенсаторами; графы «Тип, марка» и «Код продукции» для неё не заполняются (ГОСТ 21.110-2013).
4. Покупные изделия — аналог по характеристикам: заменять только на изделия не больше указанного габарита и того же материала и цвета.
5. Материал и цвет, не указанные в данных изделия, приняты по концепции (лист 17): тон дерева — по полу, обивка — по вторичному цвету палитры; образцы согласовать до заказа.
6. Масса 1 ед. для изделий до 25 кг не указывается. Техника — по монтажным схемам изготовителя; выводы — по листам ЭОМ и ВК.

Допущения и предложения на листе

Основа листа: размеры сняты с плана заказчика, контрольный обмер не выполнен (К-5); высота потолка 2700 мм принята: на плане заказчика не указана (К-5); подрайон климата не задан — принят не северный (жилые от 2,5 м) (К-4); толщины стен приняты: наружные 250 мм, перегородки 120 мм — не обмерены (К-5); разрешённая мощность 15 кВт принята по типовой квартире, технических условий нет (К-6).

Знак «**» — предложение проектировщика, заказчиком не утверждено (согласовать с заказчиком): ИЗ-2: М1 — Было offset 1300…3500: торец дивана в 500 мм от стены В, правые 350 мм проёма Д-2 (3900…4800) упирались в диван; М22 — Было х 4250 — место занял диван М1 (х 4450…5400 от у 1000); К-7: М11 — место стиральной машины: вместо модуля с ящиками 400 справа от варочной; ряд до 3420, журнальный стол М21 (с х 3440) не мешает загрузке.

Изменения по листу без подписи: ИЗ-2.

См. лист открытых вопросов (лист 6, записи К-4–К-7; лист 7, запись ИЗ-2).

Изм.	Кол.уч	Лист	№ док.	Подп.	Дата
Разраб.		Кырлан А.С.			04.11.26
Пров.					
ГИП					
Н. контр.					
Утв.					

ГД-2026-006-АИ

Квартира 58 м²

Общая площадь 55,23* м² · * размеры приняты, не замерены (реестр — л. 6, 7, К-5)

Дизайн-проект интерьера

Стадия	Лист	Листов
РП	19	87

Спецификация мебели и оборудования

М б/м

Кырлан Александр Сергеевич

выпуск 04.11.2026 № 94e55e632e · стр. 21 из 96

03

Электрооборудование


Кырлан Александр Сергеевич

выпуск 04.11.2026 № 94e55e632e · стр. 22 из 96

План розеток и электровыводов

Розетки, выводы кабеля, щит · размеры в мм · высоты от чистого пола

ПРЕДВАРИТЕЛЬНО · не для производства работ · открыто пунктов: 10 (реестр — л. 6, 7)

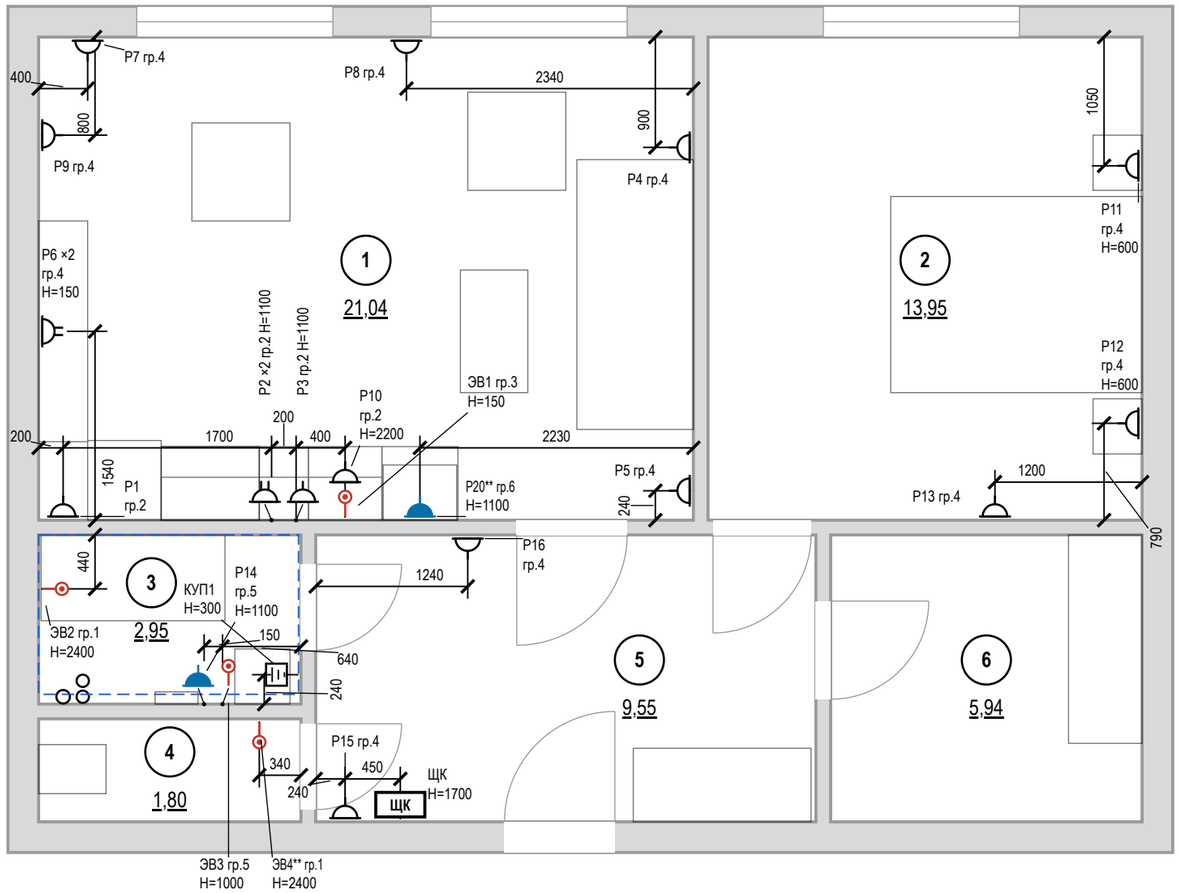

Условные обозначения

Знак	Тип изделия	Н, мм	Кол., шт
	Розетка с заземлением	300	9
	То же	у знака	4
	Блок розеток с заземлением, рамка 2 поста	у знака	2
	Розетка с заземлением IP44	1100	2
	Вывод кабеля к прибору	у знака	4
	КУП (уравнивание потенциалов)	300	1
ЩК	Щит квартирный	1700	1

розетка с заземляющим контактом; у знака — марка, ×N — постов в рамке, гр. — группа щита, Н — высота оси, мм

знак разведён для читаемости: точка на стене — у выноски, привязка — до неё

граница зоны 2 ванной (600 мм от ванны/поддона)

мебель и сантехприборы — подложка

стояк: К1 — канализация, В1 — ХВС, Т3 — ГВС

1 — номер помещения, площадь м²

Итого розеток (механизмов) — 19 шт; рамок — 17 шт: на 1 пост — 15, на 2 поста — 2.

Допущения и предложения на листе

Основа листа: размеры сняты с плана заказчика, контрольный обмер не выполнен (К-5); высота потолка 2700 мм принята: на плане заказчика не указана (К-5); подрайон климата не задан — принят не северный (жилые от 2,5 м) (К-4); толщины стен приняты: наружные 250 мм, перегородки 120 мм — не обмерены (К-5); разрешённая мощность 15 кВт принята по типовой квартире, технических условий нет (К-6).

Знак «**» — предложение проектировщика, заказчиком не утверждено (согласовать с заказчиком): ЭВ4 — вывод к бытовому вентилятору, таймер выбега; К-7: Р20 — питание стиральной машины П6 — отдельная группа 6 (УЗО 30 мА); над столешницей в габарите машины, не за корпусом.

Изменения по листу без подписи: ИЗ-1.

См. лист открытых вопросов (лист 6, записи К-4–К-7; лист 7, запись ИЗ-1).

Примечания

1. За отметку 0,000 принят уровень чистого пола. Высоты Н — от чистого пола до оси изделия; привязки — от чистовой грани стены до оси механизма (у рамки на несколько постов — до оси рамки).
2. Розетки без отметки Н у знака — на высоте 300 мм от чистого пола до оси механизма; выводы кабеля — по паспорту прибора.
3. Розетки в санузле — только вне зон 0–2 (ПУЭ 7.1.48, ГОСТ Р 50571.7.701-2024), IP44, через УЗО 30 мА.
4. Розеточные и мокрые линии — через УЗО или дифавтомат с током утечки не более 30 мА (ПУЭ 7.1.79); в санузле выполнить ДСУП (ПУЭ 7.1.87–7.1.88).
5. Кабель — медный, исполнение нг(А)-LS (ГОСТ 31565-2012); скрытая прокладка только горизонтально и вертикально, фактические трассы зафиксировать исполнительной схемой до закрытия отделкой.
6. Расчёт нагрузок, токов КЗ, селективности и сечений — по проекту ЭОМ организации с допуском СРО; лист задаёт состав, расположение и группы.
7. Выводы кухонной техники — после утверждения проекта кухни (ориентировочно); привязки выводов даны от осей модулей гарнитура и пересматриваются вместе с проектом кухни.
8. Ведомости электроточек, изделий, светильников и расшифровка клавиш — лист 23.

1000 мм · печать 1:1

Изм.	Кол.уч	Лист	№ док.	Подп.	Дата
Разраб.		Кырлан А.С.			04.11.26
Пров.					
ГИП					
Н. контр.					
Утв.					

ГД-2026-006-АИ

Квартира 58 м²

Общая площадь 55,23* м² · * размеры приняты, не замерены (реестр — л. 6, 7, К-5)

Дизайн-проект интерьера

Стадия	Лист	Листов
РП	20	87

План розеток и электровыводов

М 1:50


Кырлан Александр Сергеевич

выпуск 04.11.2026 № 94e55e632e · стр. 23 из 96

План освещения

Светильники, группы включения, извещатели · размеры в мм

ПРЕДВАРИТЕЛЬНО · не для производства работ · открыто пунктов: 10 (реестр — л. 6, 7)

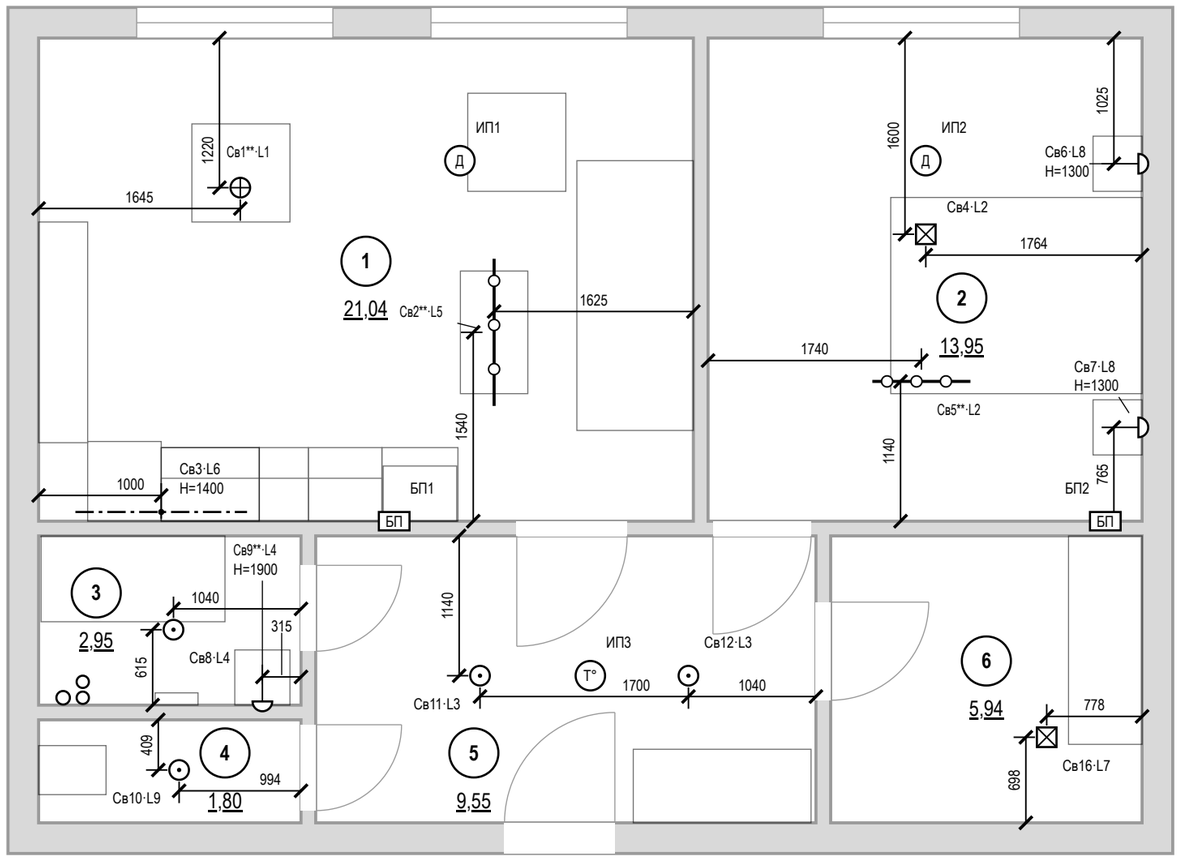

Условные обозначения

- светильник встраиваемый точечный
- светильник потолочный накладной
- светильник подвесной
- светильник настенный (бра), H — высота оси
- линейный светильник настенный (подсветка столешницы), точка — вывод питания
- трековая система
- Св1·L1 — марка светильника (как в ведомости и на развёртках) · группа включения L (лист 22)
- Д — извещатель пожарный дымовой автономный
- Т° — извещатель пожарный тепловой
- БП — блок питания LED, с доступом (люк от 100×100 мм)
- мебель и сантехприборы — подложка
- стояк: К1 — канализация, В1 — ХВС, Т3 — ГВС
- 1 — номер помещения, площадь м²

Допущения и предложения на листе

Основа листа: размеры сняты с плана заказчика, контрольный обмер не выполнен (К-5); высота потолка 2700 мм принята: на плане заказчика не указана (К-5); подрайон климата не задан — принят не северный (жилые от 2,5 м) (К-4); толщины стен приняты: наружные 250 мм, перегородки 120 мм — не обмерены (К-5); разрешённая мощность 15 кВт принята по типовой квартире, технических условий нет (К-6).

Знак «**» — предложение проектировщика, заказчиком не утверждено (согласовать с заказчиком): Св2 — общий свет зоны гостиной над журнальным столом М21 (трек шёл вдоль края стола М3 по проходу); трековая система 4 × 950 лм: поток принят до нормы освещённости, модель и паспорт не выбраны; Св5 — трековая система 2 × 900 лм: светильник добавлен проектировщиком, поток принят до нормы освещённости, модель и паспорт не выбраны; Св1 — подвес висел над проходом без заданной высоты, а стол — без света над ним: подвес по оси стола М3; Св9 — свет у зеркала — над зеркалом у умывальника по его оси (свет на лицо, а не над сантехникой).

Изменения по листу без подписи: ИЗ-1.

См. лист открытых вопросов (лист 6, записи К-4–К-6; лист 7, запись ИЗ-1).

Примечания

1. За отметку 0,000 принят уровень чистого пола. Высоты H — от чистого пола до оси изделия; привязки — от чистовой грани стены до оси механизма (у рамки на несколько постов — до оси рамки).
2. Высота установки, не указанная на плане: светильники — на потолке; настенные — по отметке H у знака. Привязки — до оси светильника от чистовой грани стены, по рядам.
3. Во влажных помещениях — светильники не ниже IP44; в зонах 0–2 ванной — по ГОСТ Р 50571.7.701-2024 (зона 1 — IPX5).
4. Розеточные и мокрые линии — через УЗО или дифавтомат с током утечки не более 30 мА (ПУЭ 7.1.79); в санузле выполнить ДСУП (ПУЭ 7.1.87–7.1.88).
5. Кабель — медный, исполнение нг(A)-LS (ГОСТ 31565-2012); скрытая прокладка только горизонтально и вертикально, фактические трассы зафиксировать исполнительной схемой до закрытия отделкой.
6. Расчёт нагрузок, токов КЗ, селективности и сечений — по проекту ЭОМ организации с допуском СРО; лист задаёт состав, расположение и группы.
7. Ведомость светильников (тип, количество, мощность, поток, Тц, Ra) — лист 39.
8. Оценка освещённости (по норме СанПиН 1.2.3685-21, табл. 5.52, на полу; не светотехнический расчёт, декоративная подсветка в оценку не входит) — лист 23.

1000 мм · печать 1:1


						ГД-2026-006-АИ	
						Квартира 58 м²	
						Общая площадь 55,23* м² · * размеры приняты, не замерены (реестр — л. 6, 7, К-5)	
Изм.	Кол.уч	Лист	№ док.	Подп.	Дата	Дизайн-проект интерьера	Стадия: РП; Лист: 21; Листов: 87
Разраб.		Кырлан А.С.			04.11.26		
Пров.							
ГИП							
						План освещения	**Кырлан Александр Сергеевич**
Н. контр.							
Утв.						М 1:50	

выпуск 04.11.2026 № 94e55e632e · стр. 24 из 96

План выключателей и схема включения

Выключатели S, группы включения L, линии связи · размеры в мм

ПРЕДВАРИТЕЛЬНО · не для производства работ · открыто пунктов: 10 (реестр — л. 6, 7)

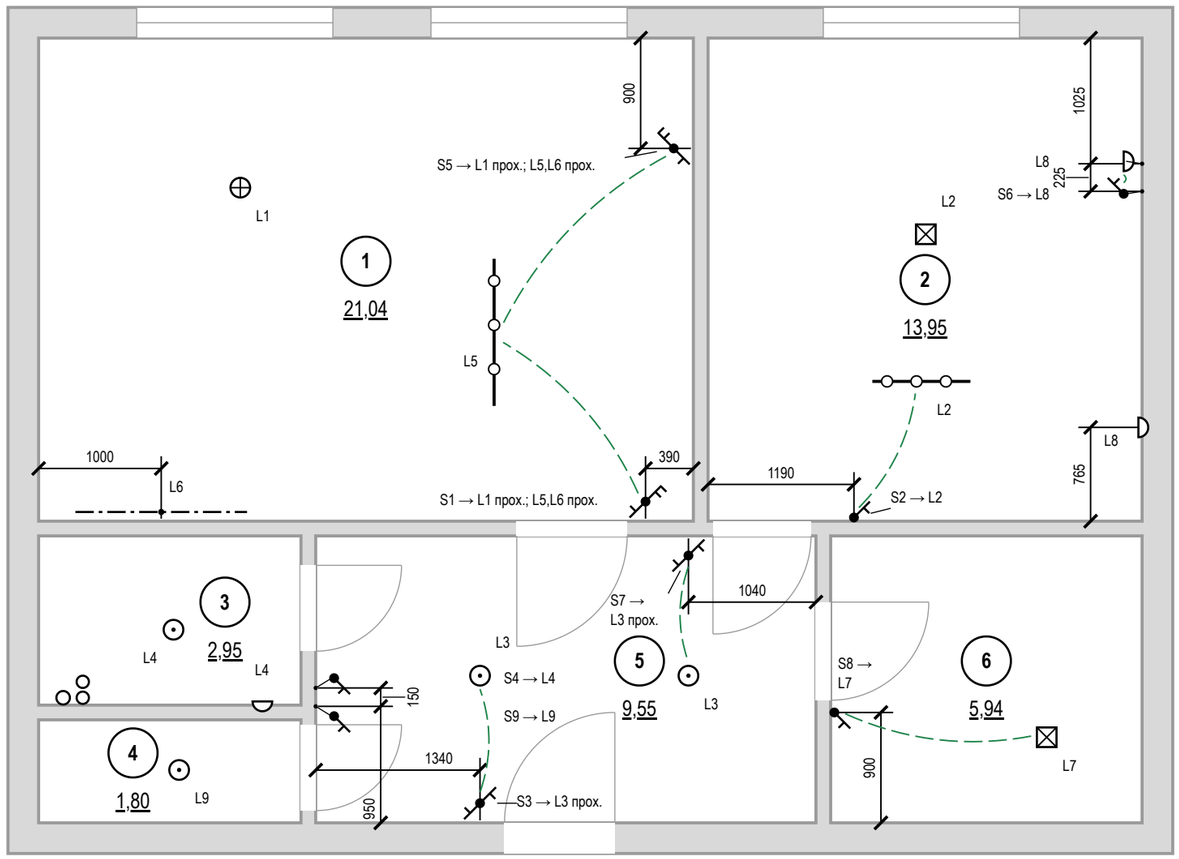

Условные обозначения

- выключатель одноклавишный
- выключатель с проходной или перекрёстной клавишей (обратный флажок); тип клавиши — в подписи
- S1 → — марка → группы по клавишам (через «;»): прох. — проходной, перекр. — перекрёстный, дим. — светорегулятор; H — высота
- связь: выключатель → ближайший светильник группы в том же помещении (не трасса кабеля); полный состав группы — по номеру L
- светильник встраиваемый точечный
- светильник потолочный накладной
- светильник подвесной
- светильник настенный (бра), H — высота оси
- линейный светильник настенный (подсветка столешницы), точка — вывод питания
- трековая система
- L1 — группа включения у светильника
- стояк: К1 — канализация, В1 — ХВС, Т3 — ГВС
- 1 — номер помещения, площадь м²

Допущения и предложения на листе

Основа листа: размеры сняты с плана заказчика, контрольный обмер не выполнен (К-5); высота потолка 2700 мм принята: на плане заказчика не указана (К-5); подрайон климата не задан — принят не северный (жилые от 2,5 м) (К-4); толщины стен приняты: наружные 250 мм, перегородки 120 мм — не обмерены (К-5); разрешённая мощность 15 кВт принята по типовой квартире, технических условий нет (К-6).

Изменения по листу без подписи: ИЗ-1.

См. лист открытых вопросов (лист 6, записи К-4–К-6; лист 7, запись ИЗ-1).

Примечания

1. За отметку 0,000 принят уровень чистого пола. Высоты H — от чистого пола до оси изделия; привязки — от чистовой грани стены до оси механизма (у рамки на несколько постов — до оси рамки).
2. Высота установки, не указанная на плане: выключатели — 900 мм от чистого пола (у кровати и другие — H у марки), со стороны дверной ручки (ПУЭ 7.1.51).
3. Какой выключатель какие светильники включает — по номеру группы L: у выключателя (S1 → L1; L2 — клавиши по порядку) и у каждого светильника. Пунктир подсказка к ближайшему светильнику группы в том же помещении (не дальше 3 м), это не трасса кабеля; выключатель за стеной (у двери санузла) и далёкая группа — только номер группы.
4. Группы из нескольких мест (L1 — S1, S5; L5 — S1, S5; L6 — S1, S5; L3 — S3, S7): на крайних местах — проходные клавиши, на промежуточных — перекрёстные; механизмы — в ведомости изделий.
5. Вентиляторы санузлов (выводы ЭВ на плане розеток) включаются вместе с основным светом помещения, отключаются с задержкой — таймер выбега в вентиляторе.
6. Розеточные и мокрые линии — через УЗО или дифавтомат с током утечки не более 30 мА (ПУЭ 7.1.79); в санузле выполнить ДСУП (ПУЭ 7.1.87–7.1.88).
7. Кабель — медный, исполнение нг(А)-LS (ГОСТ 31565-2012); скрытая прокладка только горизонтально и вертикально, фактические трассы зафиксировать исполнительной схемой до закрытия отделкой.
8. Расчёт нагрузок, токов КЗ, селективности и сечений — по проекту ЭОМ организации с допуском СРО; лист задаёт состав, расположение и группы.
9. Расшифровка клавиш и ведомость изделий — лист 23.

1000 мм · печать 1:1

Изм.	Кол.уч	Лист	№ док.	Подп.	Дата
Разраб.		Кырлан А.С.			04.11.26
Пров.					
ГИП					
Н. контр.					
Утв.					

ГД-2026-006-АИ

Квартира 58 м²

Общая площадь 55,23* м² · * размеры приняты, не замерены (реестр — л. 6, 7, К-5)

Дизайн-проект интерьера

Стадия	Лист	Листов
РП	22	87

План выключателей и схема включения

М 1:50

Кырлан Александр Сергеевич

выпуск 04.11.2026 № 94e55e632e · стр. 25 из 96

Ведомость электроточек и изделий

Электроточки, изделия, светильники, освещённость, клавиши выключателей · б/м

Ведомость электроточек

Марка	Пом.	Назначение	Н, мм	Гр.
Р1	1	холодильник	300	2
Р2	1	рабочая зона	1100	2
Р3	1	рабочая зона	1100	2
Р4	1	у дивана	300	4
Р5	1	у дивана	300	4
Р6	1	ТВ, приставка (за тумбой М20)	150	4
Р7	1	торшер	300	4
Р8	1	зона отдыха	300	4
Р9	1	обеденная зона	300	4
Р10	1	вытяжка (встроена в дно М10)	2200	2
Р20**	1	стиральная машина, IP44	1100	6
ЭВ1	1	варочная панель	150	3
Р11	2	розетка общего назначения	600	4
Р12	2	розетка общего назначения	600	4
Р13	2	комод, зарядка	300	4
КУП1	3	КУП	300	
Р14	3	фен, IP44	1100	5
ЭВ2	3	вентилятор ВР2 (клавиша L4, таймер выбега)	2400	1
ЭВ3	3	полотенцесушитель, IP44	1000	5
ЭВ4**	4	вентилятор ВР3 (таймер выбега)	2400	1
Р15	5	питание ЩС** (роутер, ИБП)	300	4
Р16	5	уборка	300	4
ЩК	5	щит квартирный	1700	

Ведомость изделий

Наименование	Марки	Ед.	Кол.
Розетка с з/к и защитными шторками, 16 А	по ведомости точек	шт	17
Розетка IP44 с крышкой, 16 А	Р14, Р20**	шт	2
Выключатель 1-клав.	S2, S4, S6, S8, S9	шт	5
Выключатель 1-клав. проходной	S3, S7	шт	2
Выключатель 2-клав. проходной	S1, S5	шт	2
Рамка 1-постовая	в т. ч. 9 под выключ.	шт	24
Рамка 2-постовая		шт	2
Коробка установочная (подрозетник) Ø68	розетки, выключатели	шт	28
Вывод кабеля под прибор (клеммник)	ЭВ1–ЭВ3	шт	3
Вывод кабеля к вентилятору вытяжки	ЭВ4**	шт	1
Коробка уравнивания потенциалов КУП	КУП1	шт	1
Блок питания LED 24 В, 100 Вт	БП1	шт	1
Блок питания LED 24 В, 60 Вт	БП2	шт	1
Извещатель дымовой автономный	ИП1, ИП2	шт	2
Извещатель тепловой	ИП3	шт	1
Щит квартирный (состав — лист щита)	ЩК	шт	1
Розетка компьютерная RJ45, кат. 6, с рамкой и подрозетником	LAN1, LAN2	шт	2
Розетка телевизионная (коаксиальная) с рамкой и подрозетником	ТВ1	шт	1
Трубка или монитор домофона (поставка домофонной организации)	ДФ1	шт	1
Щит слаботочный ЩС**: корпус, DIN-рейка, розетки 220 В	ЩС**	шт	1
Патч-панель, портов не менее 2		шт	1
Коммутатор, портов не менее 2, из них PoE 0		шт	1
Кабель домофона — тип по системе поставщика (по лучам от ЩС**, запас 10 %)		м	3,4
Кабель коаксиальный RG-6 (75 Ом) к розеткам ТВ (по лучам от ЩС**, запас 10 %)		м	16,3
Кабель U/UTP кат. 5e (LAN, Wi-Fi и камеры по PoE) (по лучам от ЩС**, запас 10 %)		м	30,1

Ведомость светильников

Поз.	Марки	Тип	Кол.	Р, Вт	Ф, лм	IP	Тц/Ra
1	Св1**	подвесной	1	40	3600		3000/90
2	Св2**	трековая система	4	12	950		3000/90
3	Св3	линейный светильник, Н=1400	1	14	1080		3000/90
4	Св4	потолочный накладной	1	36	3200		2700/90
5	Св5**	трековая система	2	12	900		2700/90
6	Св6, Св7	настенный (бра), Н=1300	2	4	250		2700/90
7	Св8	встраиваемый точечный	1	9	700	44	3000/90
8	Св9**	настенный (бра), Н=1900	1	6	400	44	3000/90
9	Св10	встраиваемый точечный	1	6	500	44	3000/90
10	Св11, Св12	встраиваемый точечный	2	9	800		3000/90
11	Св16	потолочный накладной	1	10	900		3000/90

Освещённость (оценка)

Пом.	S, м²	Ен, лк	Ф треб., лм	Ф по пр., лм
1	21	150	8890	7400
2	13,9	150	5890	5000
3	3	50	420	700
4	1,8	50	250	500
5	9,6	50	1350	1600
6	5,9	75	1250	900

Расшифровка клавиш

Марка	Пом.	Н, мм	Клав.	Механизм	Группа: светильники
S1	1	900	1	проходной	L1: Св1**
			2	проходной	L5: Св2**; L6: Св3
S2	2	900	1	обычный	L2: Св4, Св5**
S3	5	900	1	проходной	L3: Св11, Св12
S4	5	900	1	обычный	L4: Св8, Св9**
S5	1	900	1	проходной	L1: Св1**
			2	проходной	L5: Св2**; L6: Св3
S6	2	900	1	обычный	L8: Св6, Св7

Расшифровка клавиш (продолжение)

Марка	Пом.	Н, мм	Клав.	Механизм	Группа: светильники
S7	5	900	1	проходной	L3: Св11, Св12
S8	6	900	1	обычный	L7: Св16
S9	5	900	1	обычный	L9: Св10 + ЭВ4** (вентилятор)

Допущения и предложения на листе. Основа листа: размеры сняты с плана заказчика, контрольный обмер не выполнен (К-5); высота потолка 2700 мм принята: на плане заказчика не указана (К-5); подрайон климата не задан — принят не северный (жилые от 2,5 м) (К-4); толщины стен приняты: наружные 250 мм, перегородки 120 мм — не обмерены (К-5); разрешённая мощность 15 кВт принята по типовой квартире, технических условий нет (К-6). Знак «**» — предложение проектировщика, заказчиком не утверждено (согласовать с заказчиком): Св2 — общий свет зоны гостиной над журнальным столом М21 (трек шёл вдоль края стола М3 по проходу); трековая система 4 × 950 лм: поток принят до нормы освещённости, модель и паспорт не выбраны; Св5 — трековая система 2 × 900 лм: светильник добавлен проектировщиком, поток принят до нормы освещённости, модель и паспорт не выбраны; Св1 — подвес висел над проходом без заданной высоты, а стол — без света над ним: подвес по оси стола М3; Св9 — свет у зеркала — над зеркалом у умывальника по его оси (свет на лицо, а не над сантехникой); ЩС — щит слаботочный: место и состав; ЭВ4 — вывод к бытовому вентилятору, таймер выбега; К-7: Р20 — питание стиральной машины П6 — отдельная группа 6 (УЗО 30 мА); над столешницей в габарите машины, не за корпусом. См. лист открытых вопросов (лист 6, записи К-4–К-7).

Примечания

1. Ведомости сведены с планов розеток, освещения и выключателей; марки, группы и высоты — те же, что у знаков на планах.
2. Механизмы, рамки и светорегуляторы — одной серии; число постов и клавиш сверено с выбранной серией. Перекрёстная клавиша — отдельный механизм серии.
3. Освещённость (оценка) — по норме СанПиН 1.2.3685-21 (табл. 5.52, на полу), не светотехнический расчёт; декоративная подсветка в оценку не входит.
4. За отметку 0,000 принят уровень чистого пола. Высоты Н — от чистого пола до оси изделия; привязки — от чистовой грани стены до оси механизма (у рамки на несколько постов — до оси рамки).
5. Розеточные и мокрые линии — через УЗО или дифавтомат с током утечки не более 30 мА (ПУЭ 7.1.79); в санузле выполнить ДСУП (ПУЭ 7.1.87–7.1.88).
6. Кабель — медный, исполнение нг(A)-LS (ГОСТ 31565-2012); скрытая прокладка только горизонтально и вертикально, фактические трассы зафиксировать исполнительной схемой до закрытия отделкой.
7. Расчёт нагрузок, токов КЗ, селективности и сечений — по проекту ЭОМ организации с допуском СРО; лист задаёт состав, расположение и группы.

Изм.	Кол.уч	Лист	№ док.	Подп.	Дата
Разраб.		Кырлан А.С.			04.11.26
Пров.					
ГИП					
Н. контр.					
Утв.					

ГД-2026-006-АИ

Квартира 58 м²

Общая площадь 55,23* м² · * размеры приняты, не замерены (реестр — л. 6, 7, К-5)

Дизайн-проект интерьера

Стадия	Лист	Листов
РП	23	87


Ведомость электроточек и изделий

М б/м

Кырлан Александр Сергеевич

Однолинейная схема щита

Щит квартирный ЩК · без масштаба

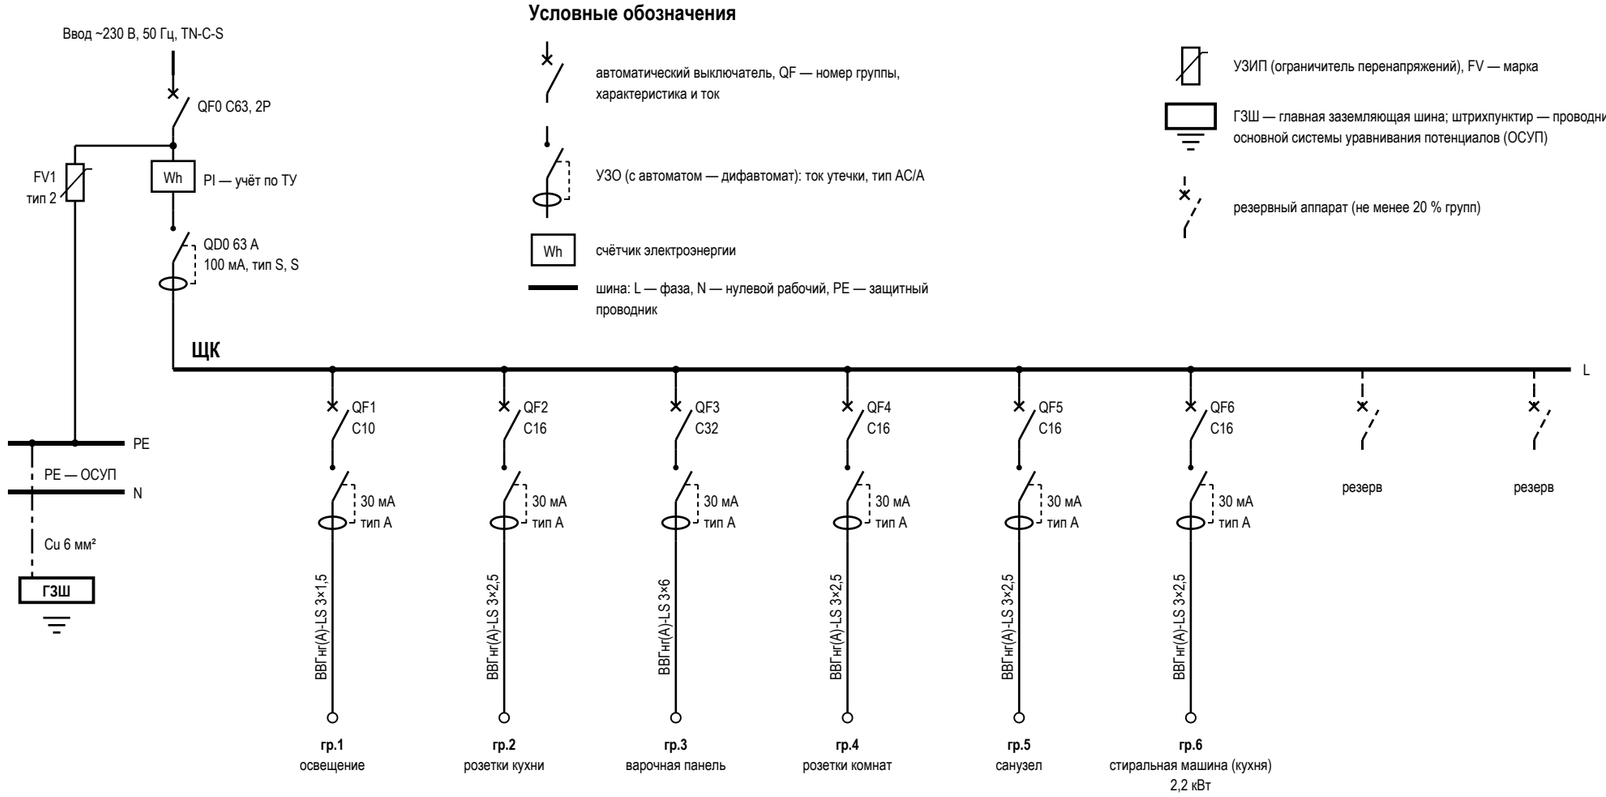

Условные обозначения

- автоматический выключатель, QF — номер группы, характеристика и ток
- УЗО (с автоматом — дифавтомат): ток утечки, тип AC/A
- Wh — счётчик электроэнергии
- шина: L — фаза, N — нулевой рабочий, PE — защитный проводник
- УЗИП (ограничитель перенапряжений), FV — марка
- ГЗШ — главная заземляющая шина; штрихпунктир — проводник основной системы уравнивания потенциалов (ОСУП)
- резервный аппарат (не менее 20 % групп)

Данные щитка

Показатель	Значение
Номер щитка	ЩК
Тип	ЩРВ-П-24, IP41
Уст. мощность, кВт	
Разреш. мощность, кВт	15
Расчётная, кВт	9,8
Автоматы 1п: занят. / рез.	6 / 2
Модулей: всего / занято	24 / 19
Ток на вводе, А	63
Вводной аппарат	QF0 C63, 2P
УЗИП	FV1, тип 2, ЩК, после счётчика
ГЗШ, проводник ОСУП	Cu 6 мм²

Таблица групп щита ЩК и кабельный журнал

№	Назначение	Помещения	Автомат	УЗО / дифавтомат	Кабель	Длина, м	Р, кВт	Точек
1	освещение	1, 2, 3, 4, 5, 6	C10	30 мА, тип A	ВВГнг(A)-LS 3×1,5	105,4		25
2	розетки кухни	1	C16	30 мА, тип A	ВВГнг(A)-LS 3×2,5	20,8		4
3	варочная панель	1	C32	30 мА, тип A	ВВГнг(A)-LS 3×6	10,7		1
4	розетки комнат	1, 2, 5	C16	30 мА, тип A	ВВГнг(A)-LS 3×2,5	48,1		11
5	санузел	3	C16	30 мА, тип A	ВВГнг(A)-LS 3×2,5	12		2
6	стиральная машина (кухня)	1	C16	30 мА, тип A	ВВГнг(A)-LS 3×2,5	11	2,2	1
	Итого по сечениям ВВГнг(A)-LS, м: 3×1,5 — 105,4; 3×2,5 — 91,9; 3×6 — 10,7					208		

Примечания

1. Схема однолинейная: одна линия — фаза, N и PE группы; аппараты — в отключённом положении (ГОСТ 2.702, ГОСТ 2.755). Номера групп — как у точек на планах (гр.). За отметку 0,000 принят уровень чистого пола; высота щита — по плану розеток.
2. Розеточные и мокрые линии — через УЗО или дифавтомат с током утечки не более 30 мА (ПУЭ 7.1.79); в санузле выполнить ДСУП (ПУЭ 7.1.87–7.1.88).
3. УЗО тип A — для линий с электроникой, стиральной и посудомоечной машиной, LED-драйверами; тип AC — только для чисто активной нагрузки.
4. Кабель — медный, исполнение нг(A)-LS (ГОСТ 31565-2012); скрытая прокладка только горизонтально и вертикально, фактические трассы зафиксировать исполнительной схемой до закрытия отделкой.
5. Номинал автомата — не выше допустимого тока кабеля: 1,5 мм² — до 10 А, 2,5 мм² — до 16 А. Резерв щита — не менее 20 % модулей.
6. Расчёт нагрузок, токов КЗ, селективности и сечений — по проекту ЭОМ организации с допуском СРО; лист задаёт состав, расположение и группы.
7. УЗИП FV1 — после вводного автомата, проводник к шине PE — кратчайший, без петель. Шина PE щита соединяется с ГЗШ проводником ОСУП; к ГЗШ присоединяются трубы водопровода и отопления на вводе в квартиру (ПУЭ 7.1.87). Шины N и PE — раздельные, после разделения PEN не объединяются.
8. До подключения нагрузки — приёмо-сдаточные испытания с протоколом: сопротивление изоляции линий не менее 0,5 МОм, срабатывание УЗО по току и времени, непрерывность защитных проводников PE (ПУЭ, гл. 1.8).

Допущения и предложения на листе

Основа листа: размеры сняты с плана заказчика, контрольный обмер не выполнен (К-5); высота потолка 2700 мм принята: на плане заказчика не указана (К-5); подрайон климата не задан — принят не северный (жилые от 2,5 м) (К-4); толщины стен приняты: наружные 250 мм, перегородки 120 мм — не обмерены (К-5); разрешённая мощность 15 кВт принята по типовой квартире, технических условий нет (К-6).

Открытые вопросы и конфликты по листу: К-6, К-7.

См. лист открытых вопросов (лист 6, записи К-4–К-7).

Изм.	Кол.уч	Лист	№ док.	Подп.	Дата
Разраб.		Кырлан А.С.			04.11.26
Пров.					
ГИП					
Н. контр.					
Утв.					

ГД-2026-006-АИ

Квартира 58 м²

Общая площадь 55,23* м² · * размеры приняты, не замерены (реестр — л. 6, 7, К-5)

Дизайн-проект интерьера

Стадия	Лист	Листов
РП	24	87

Однолинейная схема щита

М б/м


Кырлан Александр Сергеевич

выпуск 04.11.2026 № 94e55e632e · стр. 27 из 96

План принципиальных трасс

Силовые трассы и объёмы электромонтажа, слаботочка в объёмах · размеры в мм

ПРЕДВАРИТЕЛЬНО · не для производства работ · открыто пунктов: 10 (реестр — л. 6, 7)

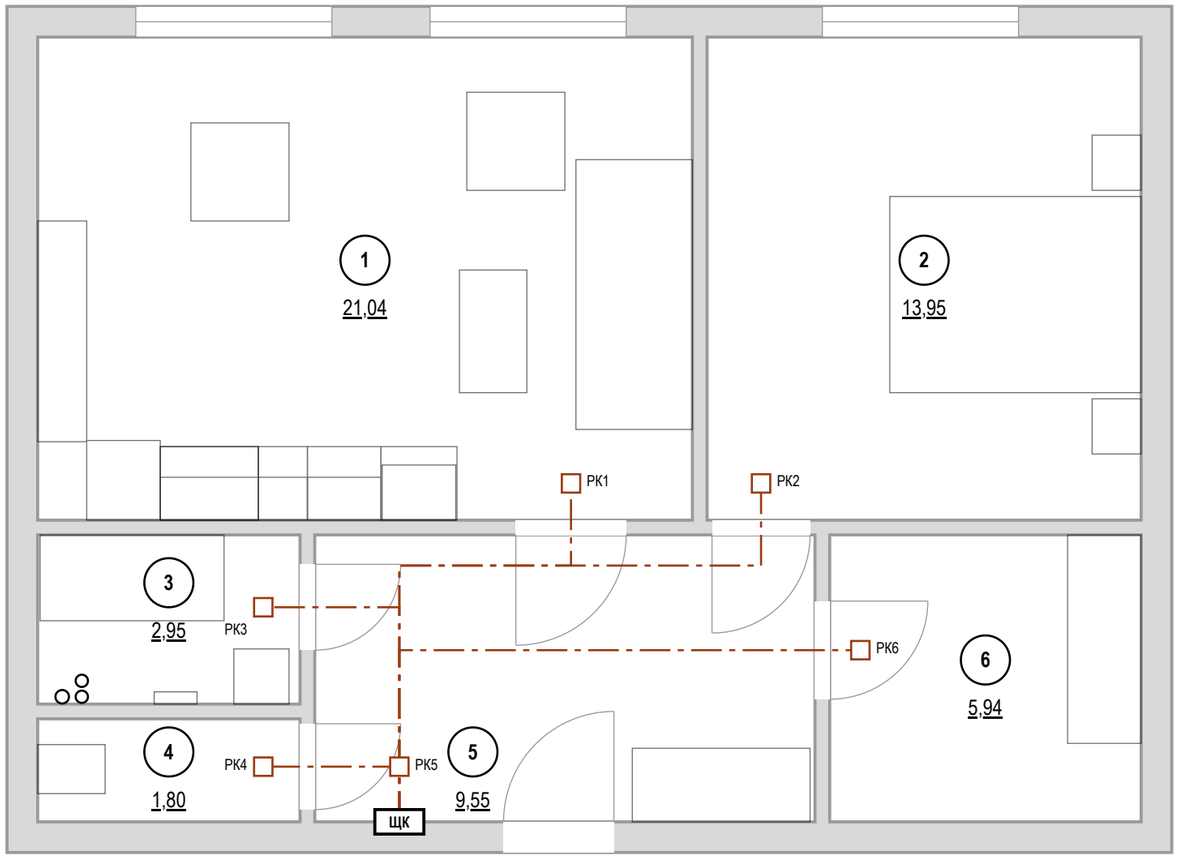

Допущения и предложения на листе

Основа листа: размеры сняты с плана заказчика, контрольный обмер не выполнен (К-5); высота потолка 2700 мм принята: на плане заказчика не указана (К-5); подрайон климата не задан — принят не северный (жилые от 2,5 м) (К-4); толщины стен приняты: наружные 250 мм, перегородки 120 мм — не обмерены (К-5); разрешённая мощность 15 кВт принята по типовой квартире, технических условий нет (К-6).

Знак «**» — предложение проектировщика, заказчиком не утверждено (согласовать с заказчиком): ЩС — щит слаботочный: место и состав.

См. лист открытых вопросов (лист 6, записи К-4–К-6).

Примечания

1. За отметку 0,000 принят уровень чистого пола. Высоты Н — от чистого пола до оси изделия; привязки — от чистовой грани стены до оси механизма (у рамки на несколько постов — до оси рамки).
2. Розеточные и мокрые линии — через УЗО или дифавтомат с током утечки не более 30 мА (ПУЭ 7.1.79); в санузле выполнить ДСУП (ПУЭ 7.1.87–7.1.88).
3. Кабель — медный, исполнение нг(А)-LS (ГОСТ 31565-2012); скрытая прокладка только горизонтально и вертикально, фактические трассы зафиксировать исполнительной схемой до закрытия отделкой.
4. Расчёт нагрузок, токов КЗ, селективности и сечений — по проекту ЭОМ организации с допуском СРО; лист задаёт состав, расположение и группы.
5. Длины — по плану: от щита вверх в потолочное пространство, по дверям и коридору без захода в мокрые помещения к распределительной коробке над дверью, далее к точкам; вертикали считаются вниз и обратно (у последней точки цепочки — в один конец); запас 10 %. Трассы принципиальные: фактическую зафиксировать исполнительной схемой до закрытия отделкой.
6. Несущие стены не определены: штробы в стенах не выполнять. Маршрут проложен без штроб: горизонтали — за потолком в гофре (72,6 м) и в кабель-канале плинтуса (54,6 м), вертикали — в коробе или накладном канале (77,8 м кабеля). Точек: за потолком — 9, спуск из потолка — 7, по плинтусу — 11, плинтус и подъём — 18.
7. Вариант со штробами — работа после технического заключения: 58,99 м вертикальных штроб от потолка до каждой настенной точки; условие — только после технического заключения: стена не несущая (или вертикальная штроба в несущей согласована конструктором), глубина и ширина 20–25 мм, не в зонах 0–2 ванной. Без заключения и согласования конструктора в смету и в график эта работа не входит.
8. Слаботочные сети: кабели и точки считаются по лучам от ЩС** (лист слаботочных сетей): 50 м, портов патч-панели и коммутатора не менее 2. Изделия — в ведомости изделий.

1000 мм · печать 1:1

Кабель по группам ВВГнг(А)-LS, м

Гр.	мм²	Трасса	Данные
1	3×1,5	105,4	
2	3×2,5	20,8	
3	3×6	10,7	

Гр.	мм²	Трасса	Данные
4	3×2,5	48,1	
5	3×2,5	12	
6	3×2,5	11	
Σ		**208**	

Экспликация помещений

№	Помещение	Площадь, м²
1	Кухня-гостиная	21,04
2	Спальня	13,95
3	Ванная	2,95
4	Санузел	1,80
5	Прихожая	9,55
6	Гардеробная	5,94
	Итого (общая площадь)	55,23

Объёмы прокладки

Работа, материал	Ед.	Кол.
Гофротруба Ø20 в потолочном пространстве	м	72,6
Кабель-канал плинтуса для силовых линий	м	54,6
Короб или накладной канал для вертикальных спусков и подъёмов	м	44,2
Коробка распределительная (РК) над дверью помещения	шт	6
Слаботочка: кабель домофона	м	3,4
Слаботочка: Кабель коаксиальный RG-6 (75 Ом) к розеткам ТВ	м	16,3
Слаботочка: Кабель U/UTP кат. 5е (LAN, Wi-Fi и камеры по PoE)	м	30,1
Слаботочка: гофротруба Ø20 отдельно от силовых	м	44,8

Штробы — только после заключения

Работа	Ед.	Кол.
Вертикальные штробы 20×20 мм от потолка до каждой настенной точки (в маршрут без штроб не входят)	м	58,99

Условные обозначения

- **ЩК** — щит квартирный
- РК — распределительная коробка над дверью помещения
- магистраль от щита к РК: потолочное пространство, гофра
- мебель и сантехприборы — подложка


Изм.	Кол.уч	Лист	№ док.	Подп.	Дата				
Разраб.		Кырлан А.С.			04.11.26	**ГД-2026-006-АИ**			
Пров.						Квартира 58 м²			
ГИП						Общая площадь 55,23* м² · * размеры приняты, не замерены (реестр — л. 6, 7, К-5)			
						Дизайн-проект интерьера	Стадия	Лист	Листов
Н. контр.							РП	25	87
Утв.						**План принципиальных трасс** М 1:50	**Кырлан Александр Сергеевич**		

выпуск 04.11.2026 № 94e55e632e · стр. 28 из 96

План слаботочных сетей

Интернет, ТВ, домофон · размеры в мм · высоты от чистого пола

ПРЕДВАРИТЕЛЬНО · не для производства работ · открыто пунктов: 10 (реестр — л. 6, 7)

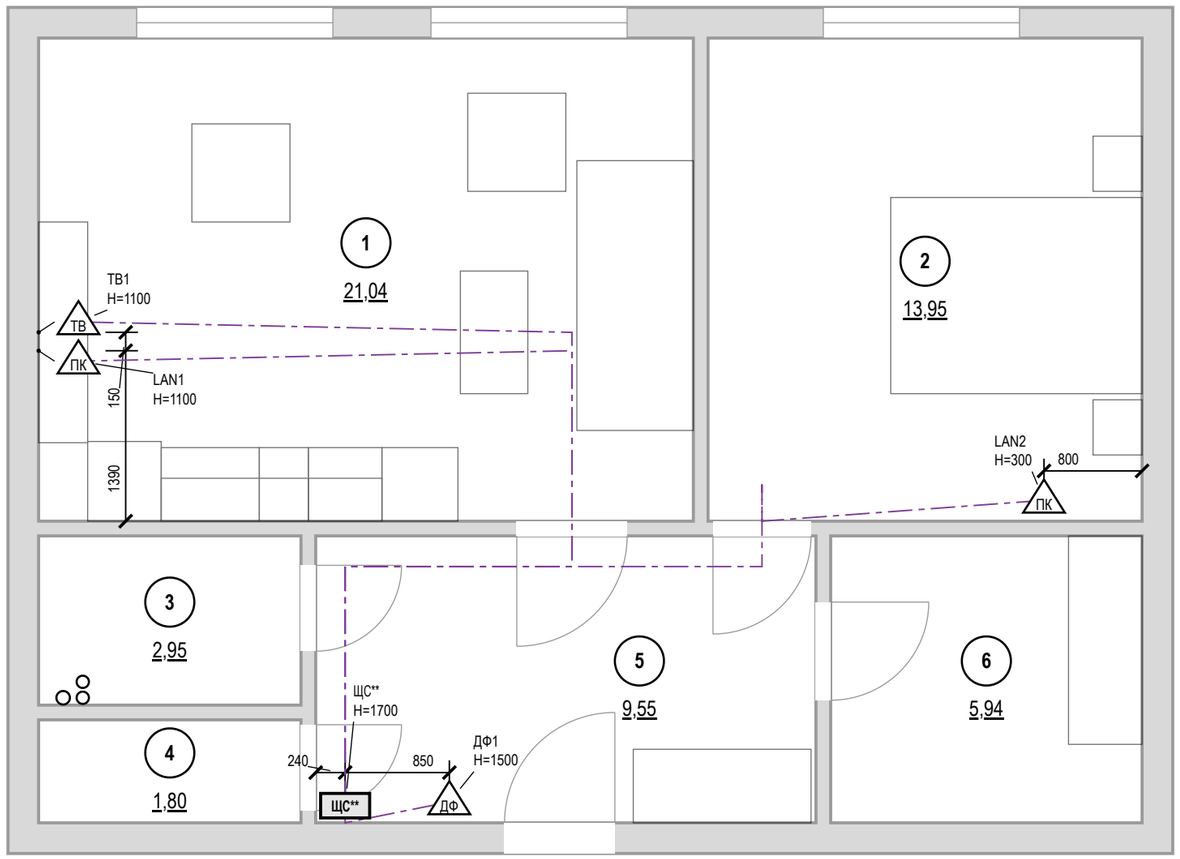

Ведомость слаботочных точек

Марка	Пом.	Назначение	H, мм	Кабель
ТВ1	1	розетка ТВ	1100	RG-6 (75 Ом)
LAN1	1	розетка LAN (RJ45)	1100	U/UTP кат. 5e/6
LAN2	2	розетка LAN (RJ45)	300	U/UTP кат. 5e/6
ЩС**	5	щит слаботочный	1700	ввод пров.
ДФ1	5	домофон (трубка)	1500	по системе

Условные обозначения

- **ЩС** — щит слаботочный: ввод провайдера, роутер, коммутатор
- ПК — розетка компьютерная RJ45
- ТВ — розетка телевизионная
- ДФ — трубка или монитор домофона
- кабель от ЩС до точки, отдельным лучом
- мебель и сантехприборы — подложка
- стояк: К1 — канализация, В1 — ХВС, Т3 — ГВС
- 1 — номер помещения, площадь м²

Допущения и предложения на листе

Основа листа: размеры сняты с плана заказчика, контрольный обмер не выполнен (К-5); высота потолка 2700 мм принята: на плане заказчика не указана (К-5); подрайон климата не задан — принят не северный (жилые от 2,5 м) (К-4); толщины стен приняты: наружные 250 мм, перегородки 120 мм — не обмерены (К-5); разрешённая мощность 15 кВт принята по типовой квартире, технических условий нет (К-6).

Знак «**» — предложение проектировщика, заказчиком не утверждено (согласовать с заказчиком): ЩС — щит слаботочный: место и состав.

См. лист открытых вопросов (лист 6, записи К-4–К-6).

Примечания

1. За отметку 0,000 принят уровень чистого пола. Высоты Н — от чистого пола до оси изделия; привязки — от чистовой грани стены до оси механизма (у рамки на несколько постов — до оси рамки).
2. Высота установки, не указанная на плане: розетки LAN и ТВ — 300 мм от чистого пола.
3. Слаботочные кабели — отдельно от силовых: в своей трубе или лотке, при параллельной прокладке не ближе 100 мм к силовым, пересечения под прямым углом; каждую точку — отдельным кабелем от ЩС** без скруток.
4. Трассы на листе — принципиальные; фактические зафиксировать исполнительной схемой до закрытия отделкой. Силовые линии, УЗО 30 мА, ДСУП, кабель нг(А)-LS — по листам розеток и щита.
5. Проект силовой части и расчёт токов КЗ — по проекту ЭОМ; слаботочная часть согласуется с провайдером и управляющей компанией (домофон, коллективное ТВ).

1000 мм · печать 1:1

Изм.	Кол.уч	Лист	№ док.	Подп.	Дата
Разраб.		Кырлан А.С.			04.11.26
Пров.					
ГИП					
Н. контр.					
Утв.					

ГД-2026-006-АИ

Квартира 58 м²

Общая площадь 55,23* м² · * размеры приняты, не замерены (реестр — л. 6, 7, К-5)

Дизайн-проект интерьера

Стадия	Лист	Листов
РП	26	87

План слаботочных сетей

М 1:50

Кырлан Александр Сергеевич

выпуск 04.11.2026 № 94e55e632e · стр. 29 из 96

04

Отопление и вентиляция

Кырлан Александр Сергеевич


выпуск 04.11.2026 № 94e55e632e · стр. 30 из 96

План вентиляции

Вытяжка, приток, переток, кондиционеры · размеры в мм · высоты от чистого пола

ПРЕДВАРИТЕЛЬНО · не для производства работ · открыто пунктов: 10 (реестр — л. 6, 7)

Допущения и предложения на листе. Основа листа: размеры сняты с плана заказчика, контрольный обмер не выполнен (К-5); высота потолка 2700 мм принята: на плане заказчика не указана (К-5); подрайон климата не задан — принят не северный (жилые от 2,5 м) (К-4); толщины стен приняты: наружные 250 мм, перегородки 120 мм — не обмерены (К-5); разрешённая мощность 15 кВт принята по типовой квартире, технических условий нет (К-6). Знак «*» — принято, не замерено и не подтверждено (замерить на объекте): КВ-2 — длина петли принята по типовому минимуму 3 м; паспорта выбранной модели нет. Знак «**» — предложение проектировщика, заказчиком не утверждено (согласовать с заказчиком): ИЗ-3: КВ-1 — длина петли принята по типовому минимуму 3 м; паспорта выбранной модели нет Внутренний блок перенесён со стены А (offset 3300…4200 — внутри оконного проёма 3200…4800) на стену Г, offset 300…1200 (простенок у окна 1, поток вдоль помещения к дивану); наружный блок КН-1 — в простенок между окнами (стена А, 2400…3200). См. лист открытых вопросов (лист 6, записи К-1, К-4–К-6; лист 7, запись ИЗ-3); по листу — К-1, ИЗ-3.

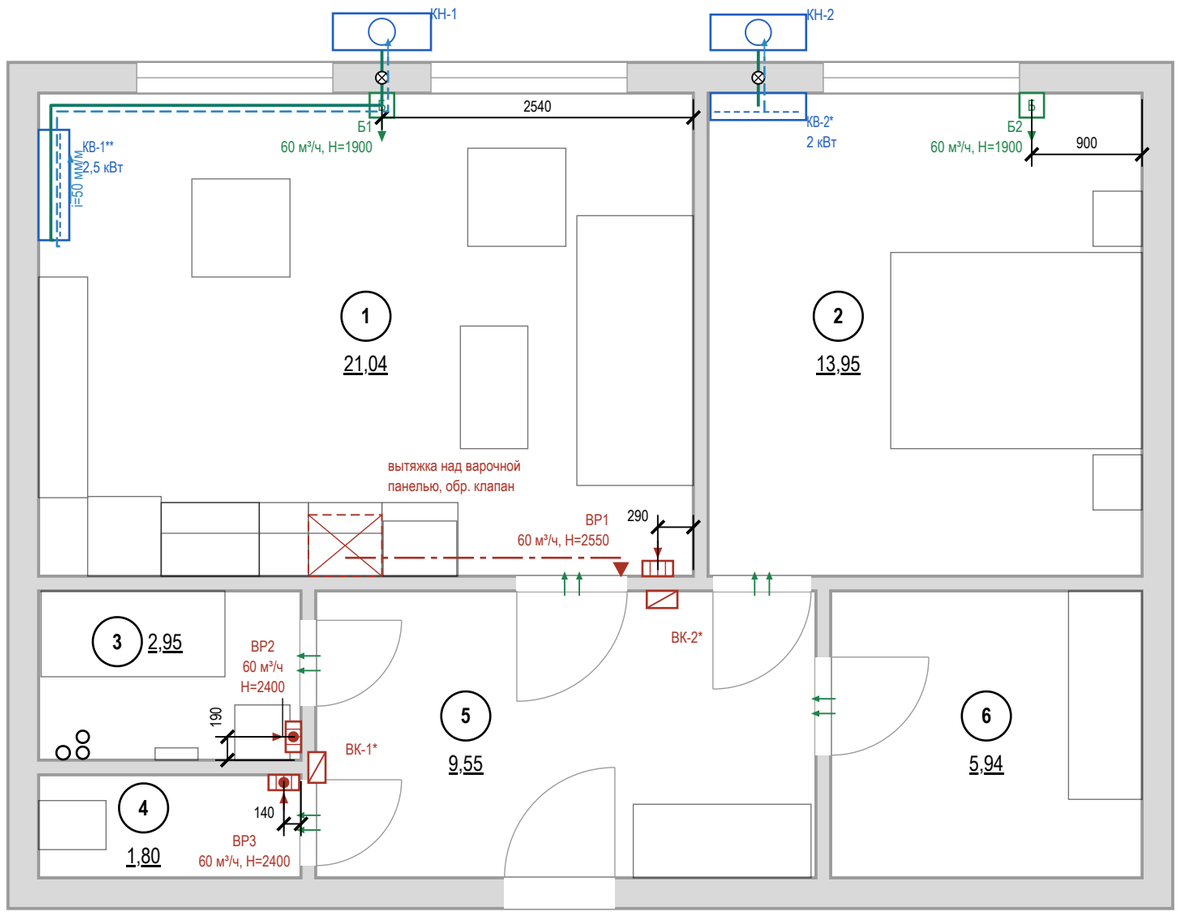

Условные обозначения

- стояк: К1 — канализация, В1 — ХВС, Т3 — ГВС
- номер помещения, площадь м²
- вытяжная решётка в вентканал: марка, расход м³/ч, Н центра от чистого пола
- вытяжная решётка с бытовым вентилятором и обратным клапаном: марка, расход, Н
- Б — бризер (приток с фильтром и подогревом)
- переток: зазор под полотном или переточная решётка
- кухонная вытяжка над варочной панелью
- вентканал ВК-N; «*» — принят до обмера
- воздуховод кухонной вытяжки в коробе под потолком
- отдельный вход воздуховода в вентканал, обратный клапан
- внутренний блок кондиционера (КВ-N)
- наружный блок (КН-N) на фасаде / в корзине
- трасса фреонопровода и межблочного кабеля
- дренаж конденсата (уклон стрелкой)
- отверстие в наружной стене под трассу

Воздухообмен, м³/ч

№	Помещение	Выт. норма	Выт. проект	Прит. норма	Прит. проект	Устрой-ства
1	Кухня-гостиная	60	60	60	60	ВР1, Б1
2	Спальня			60	60	Б2
3	Ванная	50	60			ВР2
4	Санузел	25	60			ВР3
6	Гардеробная	3				переток
	Итого	**138**	**180**	**120**	**120**	
	Норма по жильцам: 30×2			60		

Воздухообмен квартиры — по большей из сумм притока и вытяжки: норма 138 м³/ч, проект 180 м³/ч.
Вытяжка не меньше притока — баланс сведён.

Кондиционеры

Марка	Помещение	Нар. блок	Трасса, м	Дренаж
КВ-1**	1. Кухня-гостиная	КН-1	3,0	наружу, i=50 мм/м
КВ-2*	2. Спальня	КН-2	3,0 п	наружу, i=50 мм/м

Примечания

1. Расчёт систем ОВ и подбор оборудования — проектная организация с допуском СРО; лист даёт места, трассы и привязки.
2. Нормы вытяжки — СП 54.13330.2022 (Изм. 1, 2), табл. 7.1: кухня с электроплитой 60 м³/ч, с газовой 100; ванная и совмещённый санузел 50; уборная 25; гардеробная 0,2 ч⁻¹. Приток в жилые — 3 м³/ч на 1 м² (менее 20 м² общей площади на человека), иначе 30 м³/ч на человека.
3. Вентканалы и шахты не сужать, не переносить и не закрывать; вентилятор и кухонная вытяжка — через обратный клапан, без перекрытия естественной тяги.
4. Кухонная вытяжка в воздухообмен не включена: воздуховод не менее Ø125 в коробе, вход в канал отдельный.
5. Переток — зазор под полотнами межкомнатных дверей или переточная решётка.
6. Дренаж кондиционера — непрерывный уклон 40–60 мм/м без контруклонов (СТО НОСТРОЙ 2.23.1-2011, п. 5.8.4); врезка в К1 — через сифон (п. 5.8.9); длина трассы и перепад высот — по паспорту блока; внутренний блок — не ближе 150 мм к потолку, не над кроватью и рабочим местом.
7. Наружный блок на фасаде многоквартирного дома — с согласия собственников (общее имущество); при наличии корзин — только в них.
8. «п» в графе «Трасса» — трасса фреона по плану короче минимума, разница выбрана компенсационной петлёй (бухтой): КВ-2* — по плану 0,8 м, с петлёй 3,0 м. Длина петли принята по минимуму трассы (3,0 м) и зависит от паспорта модели кондиционера, которая ещё не выбрана: минимум и максимум трассы — типовые, по паспорту модели, до заказа сверить и при необходимости изменить петлю или место наружного блока. Бухту уложить в коробе или за внутренним блоком, не в штробе.
9. Привязки оборудования — по паспортам приобретённых моделей, до черновых работ.
10. Привязки — до обмера: вентканалы ВК-N* приняты проектировщиком, решётки и воздуховоды — от них. До черновых работ — обмер каналов и тяги, лист перевыпустить по факту.

1000 мм · печать 1:1

Изм.	Кол.уч	Лист	№ док.	Подп.	Дата
Разраб.		Кырлан А.С.			04.11.26
Пров.					
ГИП					
Н. контр.					
Утв.					

ГД-2026-006-АИ

Квартира 58 м²

Общая площадь 55,23* м² · * размеры приняты, не замерены (реестр — л. 6, 7, К-5)

Дизайн-проект интерьера

Стадия	Лист	Листов
РП	27	87

План вентиляции

М 1:50


Кырлан Александр Сергеевич

выпуск 04.11.2026 № 94e55e632e · стр. 31 из 96

План отопления

Радиаторы, стояки, подводки · размеры в мм · высоты от чистого пола

ПРЕДВАРИТЕЛЬНО · не для производства работ · открыто пунктов: 10 (реестр — л. 6, 7)

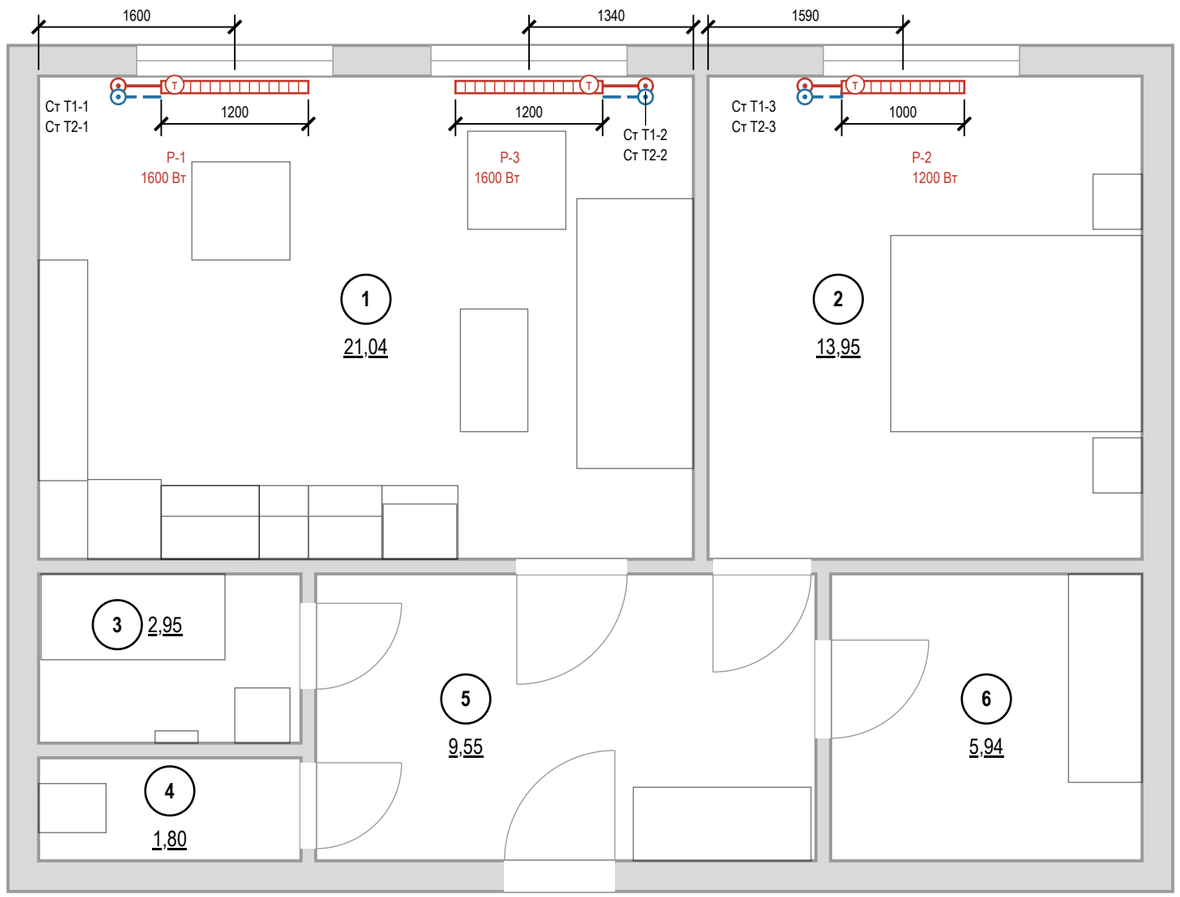

Условные обозначения

- 1 — номер помещения, площадь м²
- радиатор отопления (марка РО-N, длина по плану)
- Т — клапан с термоголовкой на подаче
- стояк отопления, подающий (Ст Т1-N)
- стояк отопления, обратный (Ст Т2-N)
- Т1 — отопление, подающий трубопровод
- Т2 — отопление, обратный трубопровод

Ведомость радиаторов

Марка	Помещение	Тип	Д×В×Г, мм	Низ / стена	Q, Вт
Р-1	1. Кухня-гостиная	панельный 22	1200×500×100	120 / 40	1600
Р-3	1. Кухня-гостиная	панельный 22	1200×500×100	120 / 40	1600
Р-2	2. Спальня	панельный 22	1000×500×100	120 / 40	1200

Низ — от чистого пола, стена — зазор до задней панели, мм.

Привязки — до обмера

Стояки отопления в исходных данных не заданы: показаны у откосов окон, подводки — принципиально. До черновых работ — обмер стояков и паспорта приборов; лист перевыпустить по факту.

Примечания

1. Расчёт системы отопления, теплопотерь и подбор приборов — проектная организация с допуском СРО; лист даёт места и привязки.
2. Тип, длина и мощность радиаторов — по теплотехническому расчёту; лист задаёт места, зазоры и подключение.
3. Зазоры радиатора: низ не менее 100 мм от чистого пола, верх не менее 100 мм до подоконника, 30–50 мм от стены до задней панели; центр по оси окна с допуском ±20 мм. Верх до подоконника — 180 мм.
4. Радиаторы не закрывать глухими коробами и мебелью; перенос и замена приборов в многоквартирном доме — переустройство, согласование с управляющей организацией (ЖК РФ ст. 25–26); вынос на лоджию запрещён.
5. Трубы отопления через межквартирные стены не прокладывать (СП 51.13330.2011, п. 9.19); через перекрытия и перегородки — в гильзах.
6. Привязки приборов и подводок — по паспортам приобретённых радиаторов и клапанов, до черновых работ.
7. До закрытия отделкой трубопроводы отопления испытать гидростатическим давлением с оформлением акта (СП 73.13330.2016, 7.2–7.3).

Допущения и предложения на листе

Основа листа: размеры сняты с плана заказчика, контрольный обмер не выполнен (К-5); высота потолка 2700 мм принята: на плане заказчика не указана (К-5); подрайон климата не задан — принят не северный (жилые от 2,5 м) (К-4); толщины стен приняты: наружные 250 мм, перегородки 120 мм — не обмерены (К-5); разрешённая мощность 15 кВт принята по типовой квартире, технических условий нет (К-6).

См. лист открытых вопросов (лист 6, записи К-4–К-6).

1000 мм · печать 1:1

Изм.	Кол.уч	Лист	№ док.	Подп.	Дата
Разраб.		Кырлан А.С.			04.11.26
Пров.					
ГИП					
Н. контр.					
Утв.					

ГД-2026-006-АИ

Квартира 58 м²

Общая площадь 55,23* м² · * размеры приняты, не замерены (реестр — л. 6, 7, К-5)

Дизайн-проект интерьера

Стадия	Лист	Листов
РП	28	87

План отопления

М 1:50

Кырлан Александр Сергеевич

выпуск 04.11.2026 № 94e55e632e · стр. 32 из 96

05

Водоснабжение и канализация

Кырлан Александр Сергеевич


выпуск 04.11.2026 № 94e55e632e · стр. 33 из 96

План выводов сантехники


Выводы В1, Т3, К1 · привязки от чистовых стен · высоты от чистого пола, мм

ПРЕДВАРИТЕЛЬНО · не для производства работ · открыто пунктов: 10 (реестр — л. 6, 7)


Фрагмент 1. Кухня-гостиная (пом. 1)

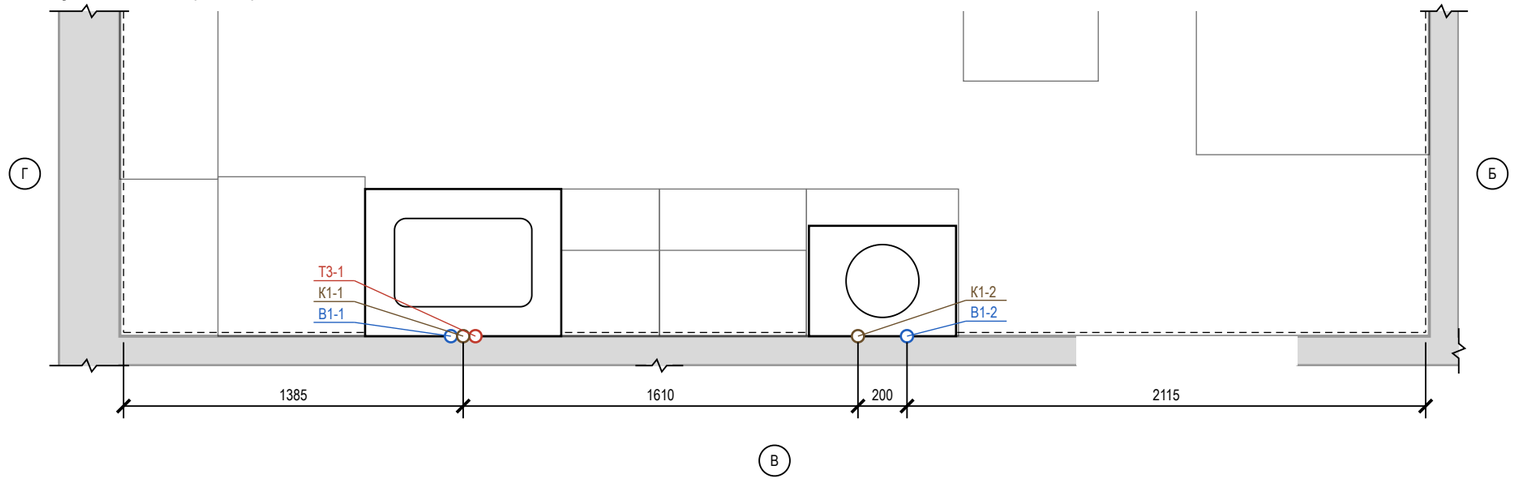

Фрагмент 2. Ванная (пом. 3)

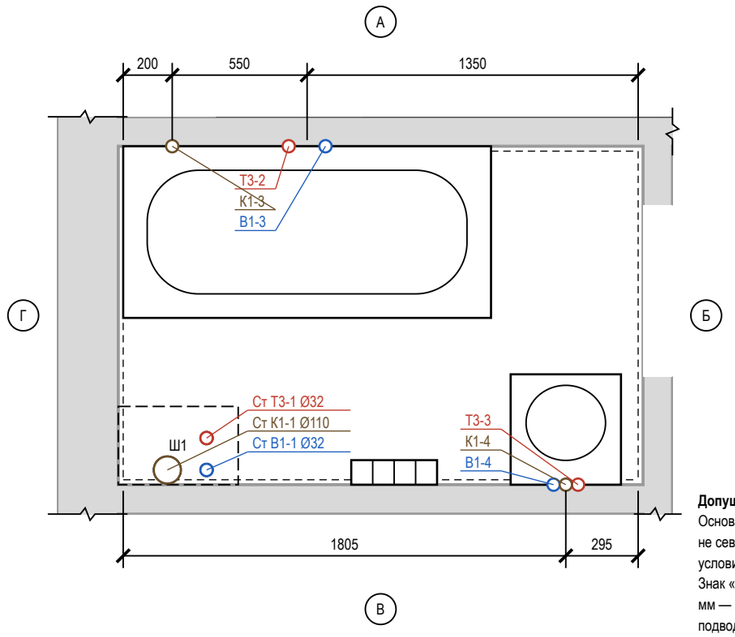

Фрагмент 3. Санузел (пом. 4)

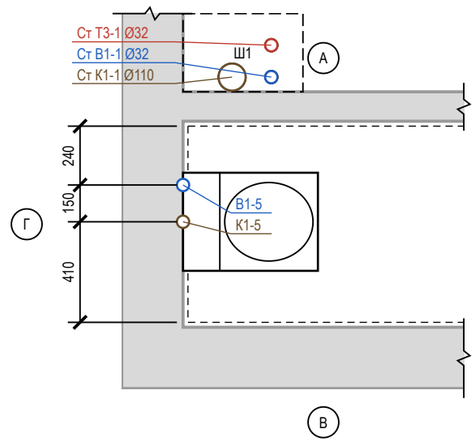

Ведомость привязок выводов

Код	Прибор	Ø	Н, мм	Привязка от чист. стен, мм	Прим.
В1-1	П4 мойка кухонная	½"	550	ст. В: 1335 от Г	межос. 100
Т3-1	П4 мойка кухонная	½"	550	ст. В: 1435 от Г	межос. 100
К1-1	П4 мойка кухонная	Ø50	400	ст. В: 1385 от Г	
В1-2	П6** стиральная машина	½"	600	ст. В: 2115 от Б	кран машины
К1-2	П6** стиральная машина	Ø40	600	ст. В: 2315 от Б	
В1-3	П1** ванна	½"	800	ст. А: 825 от Г	межос. 150
Т3-2	П1** ванна	½"	800	ст. А: 675 от Г	межос. 150
К1-3	П1** ванна	Ø50	50	ст. А: 200 от Г	
В1-4	П3** умывальник	½"	550	ст. В: 345 от Б	межос. 100
Т3-3	П3** умывальник	½"	550	ст. В: 245 от Б	межос. 100
К1-4	П3** умывальник	Ø50	500	ст. В: 295 от Б	
В1-5	П20 унитаз подвесной	½"	150	ст. Г: 240 от А	в раме инсталляции
К1-5	П20 унитаз подвесной	Ø110	230	ст. Г: 390 от А	

* — высота по практике монтажа; сверить по паспорту прибора

Условные обозначения

- вывод В1 (код — в ведомости привязок)
- вывод Т3 (код — в ведомости привязок)
- вывод К1 (код — в ведомости привязок)
- сантехприбор по расстановке (габарит модели)
- чистовая поверхность стены (от неё привязки)
- стояк «Ст К1-N / Ст В1-N» (ГОСТ 21.601), Ø мм
- шахта / короб стояков, люк 300×400
- линия обрыва (граница фрагмента)
- А — обозначение стены А–Г (как на развёртках)

Допущения и предложения на листе

Основа листа: размеры сняты с плана заказчика, контрольный обмер не выполнен (К-5); высота потолка 2700 мм принята: на плане заказчика не указана (К-5); подрайон климата не задан — принят не северный (жилые от 2,5 м) (К-4); толщины стен приняты: наружные 250 мм, перегородки 120 мм — не обмерены (К-5); разрешённая мощность 15 кВт принята по типовой квартире, технических условий нет (К-6).

Знак «**» — предложение проектировщика, заказчиком не утверждено (согласовать с заказчиком): К-2: П1 — ванна 1500 вместо 1600 — не заходит в проход перед проёмом Д-4; перед ванной 680 мм — глубина помещения; П3 — умывальник у стены В справа от ванны — перед ним свободно 750 мм, до стены Б 90 мм; К-7: П6 — стиральная машина на кухне: в ванной и санузле места нет; подвод ХВС с шаровым краном, слив — встраиваемый сифон с обратным клапаном (водяной затвор), отдельная группа 6 щита с УЗО 30 мА.

Открытые вопросы и конфликты по листу: К-2, К-7.

См. лист открытых вопросов (лист 6, записи К-2, К-4–К-7).

Примечания

1. Привязки выводов даны от чистовых поверхностей стен (облицовка на сторону: кухня-гостиная — 15 мм (по данным); ванная — 20 мм (по данным); санузел — 20 мм (по данным)); эти же грани — на развёртках и в раскладке плитки. Высоты — от чистого пола помещения.
2. Высоты и межосевые, отмеченные «*», приняты по практике монтажа; до черновой разводки сверить по паспорту выбранного прибора (смеситель, инсталляция, сифон).
3. Горячая вода (Т3) — слева от холодной (В1), если смотреть на прибор. Допуск установки выводов: ±5 мм в группе, ±20 мм у отдельно стоящих.
4. Расчёт систем водоснабжения и канализации и подбор оборудования выполняет проектная организация; лист задаёт места и высоты выводов.
5. Стояки в коробах/шахтах Ш1 не замоноличивать; стояк К1 в коробе — звукоизоляция стояка в коробе без жёсткого контакта с трубой; к арматуре и ревизиям — люк не меньше 300×400.

1000 мм · печать 1:1

Изм.	Кол.уч	Лист	№ док.	Подп.	Дата
Разраб.		Кырлан А.С.			04.11.26
Пров.					
ГИП					
Н. контр.					
Утв.					

ГД-2026-006-АИ

Квартира 58 м²

Общая площадь 55,23* м² · * размеры приняты, не замерены (реестр — л. 6, 7, К-5)

Дизайн-проект интерьера

Стадия	Лист	Листов
РП	29	87

План выводов сантехники

М 1:25

Кырлан Александр Сергеевич


выпуск 04.11.2026 № 94e55e632e · стр. 34 из 96

Схема разводки водопровода и канализации


Схемы систем В1, Т3, К1 · трассы принципиальные · уклоны в мм на 1 м · план М 1:200, фрагменты М 1:25

ПРЕДВАРИТЕЛЬНО · не для производства работ · открыто пунктов: 10 (реестр — л. 6, 7)


План квартиры (М 1:200)

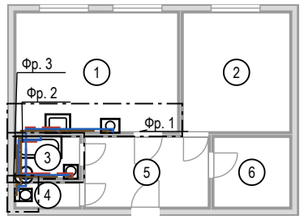


Фр. 1. Кухня-гостиная (М 1:25)

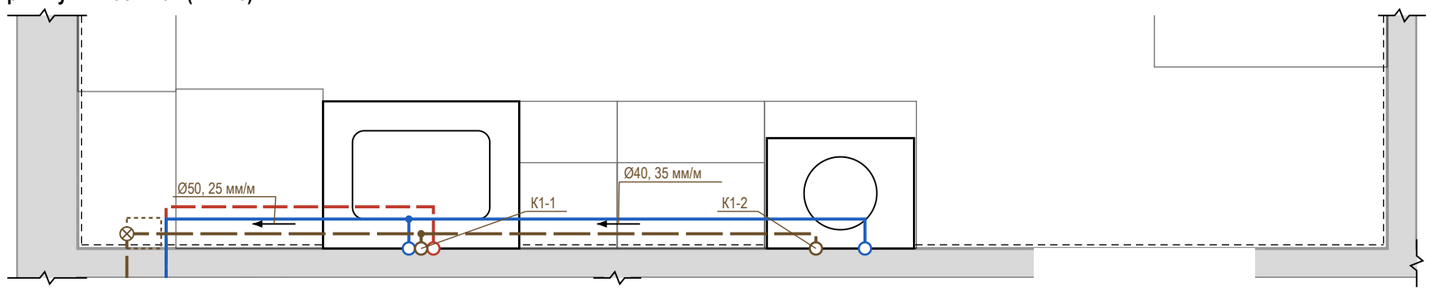

Фр. 2. Ванная (М 1:25)

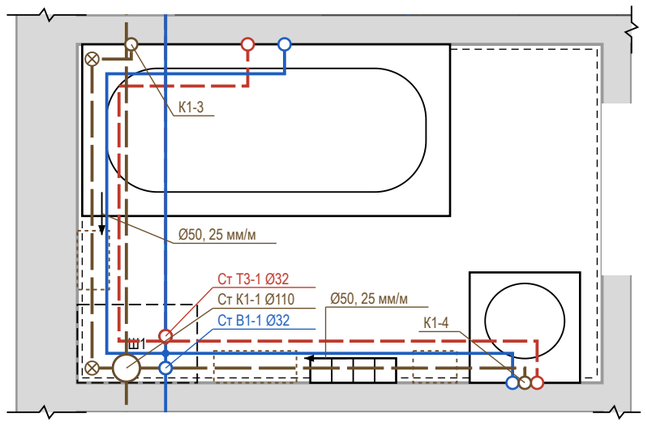

Фр. 3. Санузел (М 1:25)

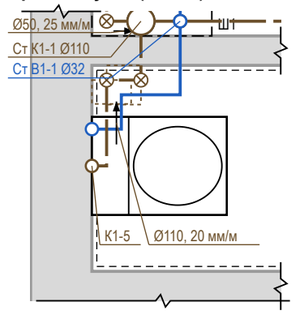

Условные обозначения

- В1 — водопровод хозяйственно-питьевой (ХВС), PP-R Ø20
- Т3 — горячее водоснабжение, подача (ГВС), PP-R Ø20
- К1 — канализация бытовая
- направление уклона К1 / пола: Ø, мм на 1 м
- ревизия (прочистка) К1 — доступ сохранить
- тройник (ответвление к прибору)
- короб К1 над чистым полом (ГКЛВ под плитку)
- вывод В1 (код — в ведомости привязок)
- вывод Т3 (код — в ведомости привязок)
- вывод К1 (код — в ведомости привязок)
- сантехприбор по расстановке (габарит модели)
- стояк «Ст К1-N / Ст В1-N» (ГОСТ 21.601), Ø мм
- шахта / короб стояков, люк 300×400
- линия обрыва (граница фрагмента)
- граница фрагмента на плане (Фр. N)

Профиль выпусков К1 (до врезки в стояк)

Выпуск	Прибор	Ø	L, м	i, мм/м	Δh, мм	Прокладка, мм
К1-5	П20 унитаз подвесной	Ø110	0,79	20	16	короб 160×140
К1-1	П4 мойка кухонная	Ø50	2,76	25	69	короб 150×110
К1-4	П3** умывальник	Ø50	1,69	25	42	короб 130×110
К1-3	П1** ванна	Ø50	1,62	25	41	короб 130×110
К1-2	П6** стиральная машина	Ø40	4,37	35	153	короб 230×110

Короб h×b: h — от чистого пола, b — от чистовой стены. Стяжка 90 мм — лист полов.

Узел ввода В1, Т3 (схема, без масштаба)



состав узла — по согласованию

⊗ Ст К1-1: ревизия на стояке — люк в коробе

Примечания

1. Трассы принципиальные, построены от стояков вдоль стен помещений; фактическое положение фиксируется исполнительной схемой с привязками (фото с рулеткой) до закрытия.
2. Уклон К1 не менее 1/d и не более 150 мм/м (СП 30.13330.2020, п. 19.1), приняты практические уклоны; поворот — двумя отводами 45°, ревизия после поворота, доступ сохранить. Стояк К1 в коробе — звукоизоляция стояка в коробе, без жёсткого контакта короба с трубой.
3. Решение по К1: стяжка 90 мм не укрывает трубы (нужно Ø + Δh + 45 мм) — выпуски идут над чистым полом вдоль стен; К1-5, К1-1, К1-4, К1-3, К1-2 — в коробе ГКЛВ под плитку (размеры в профиле). Короба — на развёртках; отметку низа врезки в стояк замерить до черновых работ.
4. Отводы К1-2 (4,4 м) длиннее 4 м без вентиляции — у прибора воздушный клапан Ø50 в доступном месте (за люком или в тумбе) либо вентилируемый отвод (EN 12056-2, табл. 4); предложение проектировщика, подбор — проектная организация.
5. Состав узла ввода В1, Т3 — по согласованию: на схеме типовой узел — кран шаровой, фильтр, счётчик, обратный клапан, кран; состав и места не определены (записи реестра нет). Доступ к арматуре — через люк не меньше 300×400. Водопровод — в штробе стен или в коробах; трубы испытать давлением до закрытия (акт скрытых работ).
6. Расчёт систем, диаметры магистралей и подбор оборудования выполняет проектная организация; врезка и перенос стояков — по согласованию с управляющей организацией. Арматуру и привязки сверить по паспортам приборов.

Допущения и предложения на листе. Знак «**» предложено (согласовать). См. лист открытых вопросов (листы 6, 7).

Изм.	Кол.уч	Лист	№ док.	Подп.	Дата
Разраб.		Кырлан А.С.			04.11.26
Пров.					
ГИП					
Н. контр.					
Утв.					

ГД-2026-006-АИ

Квартира 58 м²

Общая площадь 55,23* м² · * размеры приняты, не замерены (реестр — л. 6, 7, К-5)

Дизайн-проект интерьера

Стадия	Лист	Листов
РП	30	87

Схема разводки водопровода и канализации

М 1:200; 1:25


Кырлан Александр Сергеевич

выпуск 04.11.2026 № 94e55e632e · стр. 35 из 96

Аксонометрическая схема В1 (холодное водоснабжение)

аксонометрия · диаметры, уклоны, отметки, стояки и приборы · трассы принципиальные

Схема В1 (М 1:50; по вертикали и горизонтали один масштаб, глубина — ×0,5 под 45°)

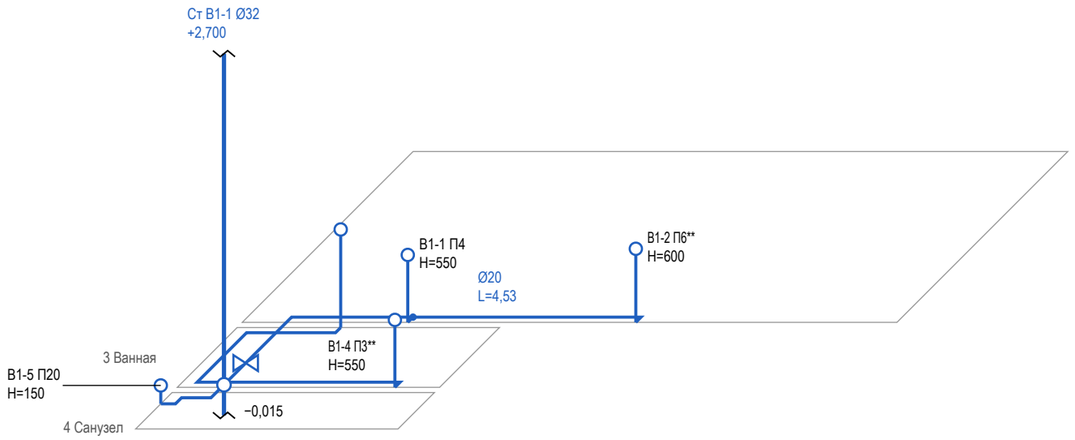

ПРЕДВАРИТЕЛЬНО · не для производства работ · открыто пунктов: 10 (реестр — л. 6, 7)

Условные обозначения

- В1 — водопровод хозяйственно-питьевой (ХВС), PP-R Ø20
- вывод В1 (код — в ведомости привязок)
- стояк «Ст К1-N / Ст В1-N» (ГОСТ 21.601), Ø мм
- стояк в плане (на отметке пола); вертикаль — стояк по высоте, разрыв — перекрытие
- тройник (ответвление к прибору)
- кран шаровой

Допущения и предложения на листе

Основа листа: размеры сняты с плана заказчика, контрольный обмер не выполнен (К-5); высота потолка 2700 мм принята: на плане заказчика не указана (К-5); подрайон климата не задан — принят не северный (жилые от 2,5 м) (К-4); толщины стен приняты: наружные 250 мм, перегородки 120 мм — не обмерены (К-5); разрешённая мощность 15 кВт принята по типовой квартире, технических условий нет (К-6).

Знак «**» — предложение проектировщика, заказчиком не утверждено (согласовать с заказчиком): К-2: П3 — умывальник у стены В справа от ванны — перед ним свободно 750 мм, до стены Б 90 мм; К-7: П6 — стиральная машина на кухне: в ванной и санузле места нет; подвод ХВС с шаровым краном, слив — встраиваемый сифон с обратным клапаном (водяной затвор), отдельная группа 6 щита с УЗО 30 мА.

См. лист открытых вопросов (лист 6, записи К-2, К-4–К-7).

Примечания

1. Схема В1 построена по тем же трассам, что план разводки: положение в плане сохранено, глубина — в масштабе ×0,5. Трассы принципиальные; фактическое положение фиксируется исполнительной схемой до закрытия.
2. Высоты Н — от чистого пола помещения, мм. Отметка прокладки магистрали В1 (в стяжке, в стене или по полу) в данных не задана: участки показаны на уровне пола условно (записи реестра нет).
3. Узел ввода В1 (кран, фильтр, счётчик, обратный клапан, кран) — на схеме разводки; состав узла ввода — по согласованию. Кран шаровой — на первом участке от стояка.
4. Трубы испытать давлением до закрытия (акт скрытых работ, опрессовка по СП 73.13330.2016).
5. Диаметры, высоты выводов и места кранов — по паспортам выбранных приборов и расчёту проектной организации.
6. Расчёт систем, диаметры магистралей и подбор оборудования выполняет проектная организация.

1000 мм · печать 1:1

Изм.	Кол.уч	Лист	№ док.	Подп.	Дата
Разраб.		Кырлан А.С.			04.11.26
Пров.					
ГИП					
Н. контр.					
Утв.					

ГД-2026-006-АИ

Квартира 58 м²

Общая площадь 55,23* м² · * размеры приняты, не замерены (реестр — л. 6, 7, К-5)

Дизайн-проект интерьера

Стадия	Лист	Листов
РП	31	87

Аксонометрическая схема В1 (холодное водоснабжение)

М 1:50


Кырлан Александр Сергеевич

выпуск 04.11.2026 № 94e55e632e · стр. 36 из 96

Аксонометрическая схема Т3 (горячее водоснабжение)

аксонометрия · диаметры, уклоны, отметки, стояки и приборы · трассы принципиальные

Схема Т3 (М 1:50; по вертикали и горизонтали один масштаб, глубина — ×0,5 под 45°)

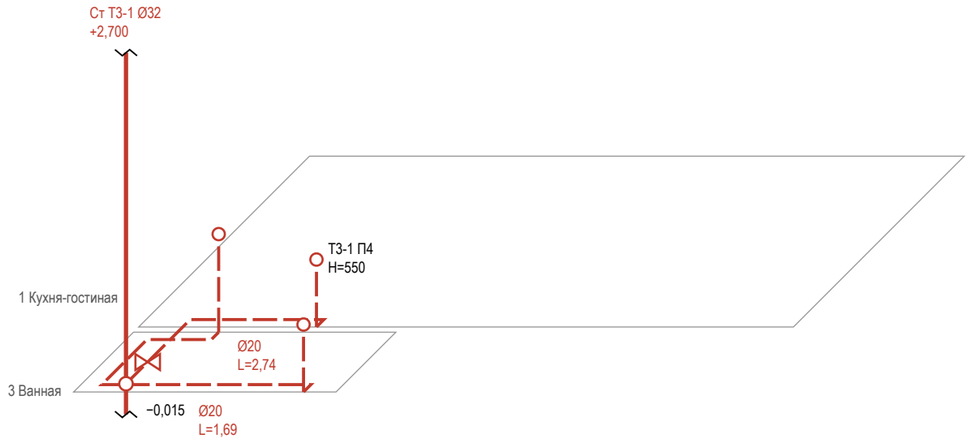

ПРЕДВАРИТЕЛЬНО · не для производства работ · открыто пунктов: 10 (реестр — л. 6, 7)

Условные обозначения

- Т3 — горячее водоснабжение, подача (ГВС), PP-R Ø20
- вывод Т3 (код — в ведомости привязок)
- стояк «Ст К1-N / Ст В1-N» (ГОСТ 21.601), Ø мм
- стояк в плане (на отметке пола); вертикаль — стояк по высоте, разрыв — перекрытие
- тройник (ответвление к прибору)
- кран шаровой

Допущения и предложения на листе

Основа листа: размеры сняты с плана заказчика, контрольный обмер не выполнен (К-5); высота потолка 2700 мм принята: на плане заказчика не указана (К-5); подрайон климата не задан — принят не северный (жилые от 2,5 м) (К-4); толщины стен приняты: наружные 250 мм, перегородки 120 мм — не обмерены (К-5); разрешённая мощность 15 кВт принята по типовой квартире, технических условий нет (К-6).

См. лист открытых вопросов (лист 6, записи К-4–К-6).

Примечания

1. Схема Т3 построена по тем же трассам, что план разводки: положение в плане сохранено, глубина — в масштабе ×0,5. Трассы принципиальные; фактическое положение фиксируется исполнительной схемой до закрытия.
2. Высоты Н — от чистого пола помещения, мм. Отметка прокладки магистрали Т3 (в стяжке, в стене или по полу) в данных не задана: участки показаны на уровне пола условно (записи реестра нет).
3. Узел ввода Т3 (кран, фильтр, счётчик, обратный клапан, кран) — на схеме разводки; состав узла ввода — по согласованию. Кран шаровой — на первом участке от стояка.
4. Циркуляция ГВС в данных не задана — циркуляционного трубопровода на схеме нет (записи реестра нет).
5. Трубы испытать давлением до закрытия (акт скрытых работ, опрессовка по СП 73.13330.2016).
6. Диаметры, высоты выводов и места кранов — по паспортам выбранных приборов и расчёту проектной организации.
7. Расчёт систем, диаметры магистралей и подбор оборудования выполняет проектная организация.

1000 мм · печать 1:1

Изм.	Кол.уч	Лист	№ док.	Подп.	Дата
Разраб.		Кырлан А.С.			04.11.26
Пров.					
ГИП					
Н. контр.					
Утв.					

ГД-2026-006-АИ

Квартира 58 м²

Общая площадь 55,23* м² · * размеры приняты, не замерены (реестр — л. 6, 7, К-5)

Дизайн-проект интерьера

Стадия	Лист	Листов
РП	32	87

Аксонометрическая схема Т3 (горячее водоснабжение)

М 1:50


Кырлан Александр Сергеевич

выпуск 04.11.2026 № 94e55e632e · стр. 37 из 96

Аксонометрическая схема К1 (канализация)

аксонометрия · диаметры, уклоны, отметки, стояки и приборы · трассы принципиальные

Схема К1 (М 1:50; по вертикали и горизонтали один масштаб, глубина — ×0,5 под 45°)

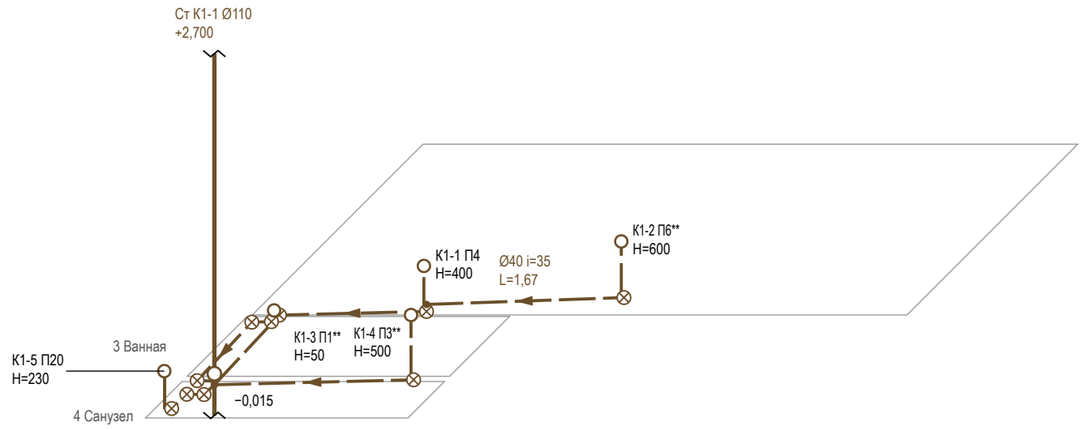

ПРЕДВАРИТЕЛЬНО · не для производства работ · открыто пунктов: 10 (реестр — л. 6, 7)

Условные обозначения

- К1 — канализация бытовая
- вывод К1 (код — в ведомости привязок)
- стояк «Ст К1-N / Ст В1-N» (ГОСТ 21.601), Ø мм
- стояк в плане (на отметке пола); вертикаль — стояк по высоте, разрыв — перекрытие
- направление уклона К1 / пола: Ø, мм на 1 м
- ревизия (прочистка) К1 — доступ сохранить
- тройник (ответвление к прибору)

Допущения и предложения на листе

Основа листа: размеры сняты с плана заказчика, контрольный обмер не выполнен (К-5); высота потолка 2700 мм принята: на плане заказчика не указана (К-5); подрайон климата не задан — принят не северный (жилые от 2,5 м) (К-4); толщины стен приняты: наружные 250 мм, перегородки 120 мм — не обмерены (К-5); разрешённая мощность 15 кВт принята по типовой квартире, технических условий нет (К-6).

Знак «**» — предложение проектировщика, заказчиком не утверждено (согласовать с заказчиком): К-2: П1 — ванна 1500 вместо 1600 — не заходит в проход перед проёмом Д-4; перед ванной 680 мм — глубина помещения; П3 — умывальник у стены В справа от ванны — перед ним свободно 750 мм, до стены Б 90 мм; К-7: П6 — стиральная машина на кухне: в ванной и санузле места нет; подвод ХВС с шаровым краном, слив — встраиваемый сифон с обратным клапаном (водяной затвор), отдельная группа 6 щита с УЗО 30 мА.

См. лист открытых вопросов (лист 6, записи К-2, К-4–К-7).

Примечания

1. Схема К1 построена по тем же трассам, что план разводки: положение в плане сохранено, глубина — в масштабе ×0,5. Трассы принципиальные; фактическое положение фиксируется исполнительной схемой до закрытия.
2. Отметки — от плиты перекрытия: низ трубы у врезки в стояк — отметка из данных выпуска, к прибору труба поднимается на уклон i, мм/м (уклон не менее 1/d и не более 150 мм/м, СП 30.13330.2020, п. 19.1); чистый пол — выше плиты на стяжку (высота пирога пола). Высота выпуска прибора H — от чистого пола.
3. Ревизия — на повороте и в начале участка; стояк К1 в коробе с люком — звукоизоляция стояка в коробе; поворот — двумя отводами 45°.
4. Трубы испытать давлением до закрытия (акт скрытых работ, опрессовка по СП 73.13330.2016).
5. Диаметры, высоты выводов и места кранов — по паспортам выбранных приборов и расчёту проектной организации.
6. Расчёт систем, диаметры магистралей и подбор оборудования выполняет проектная организация.

1000 мм · печать 1:1

Изм.	Кол.уч	Лист	№ док.	Подп.	Дата
Разраб.		Кырлан А.С.			04.11.26
Пров.					
ГИП					
Н. контр.					
Утв.					

ГД-2026-006-АИ

Квартира 58 м²

Общая площадь 55,23* м² · * размеры приняты, не замерены (реестр — л. 6, 7, К-5)

Дизайн-проект интерьера

Стадия	Лист	Листов
РП	33	87

Аксонометрическая схема К1 (канализация)

М 1:50

Кырлан Александр Сергеевич


выпуск 04.11.2026 № 94e55e632e · стр. 38 из 96

Развёртки мокрых зон: выводы ВК. Кухня-гостиная

пом. 1 · выводы В1, Т3, К1 на стенах · высоты от чистого пола, привязки от чистовых углов, мм

ПРЕДВАРИТЕЛЬНО · не для производства работ · открыто пунктов: 10 (реестр — л. 6, 7)

Стена В (М 1:20)

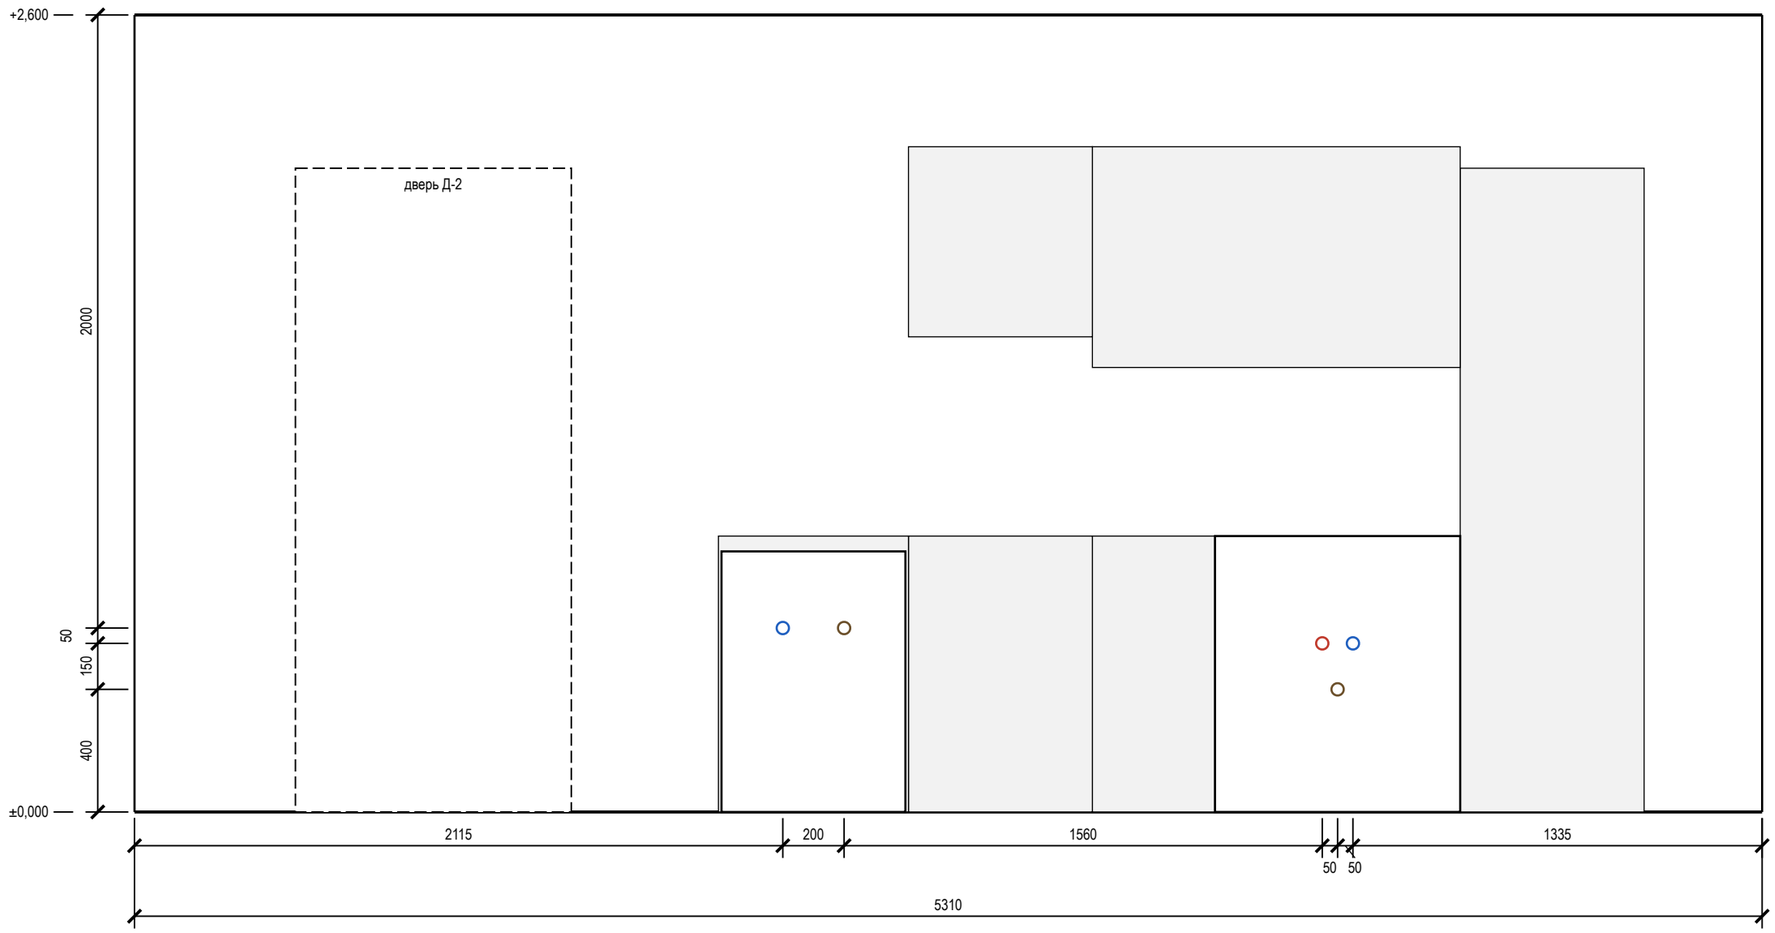

Допущения и предложения на листе

Основа листа: размеры сняты с плана заказчика, контрольный обмер не выполнен (К-5); высота потолка 2700 мм принята: на плане заказчика не указана (К-5); подрайон климата не задан — принят не северный (жилые от 2,5 м) (К-4); толщины стен приняты: наружные 250 мм, перегородки 120 мм — не обмерены (К-5); разрешённая мощность 15 кВт принята по типовой квартире, технических условий нет (К-6).

Знак «**» — предложение проектировщика, заказчиком не утверждено (согласовать с заказчиком): К-7: П6 — стиральная машина на кухне: в ванной и санузле места нет; подвод ХВС с шаровым краном, слив — встраиваемый сифон с обратным клапаном (водяной затвор), отдельная группа 6 щита с УЗО 30 мА.

См. лист открытых вопросов (лист 6, записи К-4–К-7).

Ведомость привязок выводов (от чистого пола и угла)

Код	Прибор	Ø	Н, мм	Привязка, мм
В1-1	П4 мойка кухонная	½"	550	ст. В: 3975 от лев. угла
Т3-1	П4 мойка кухонная	½"	550	ст. В: 3875 от лев. угла
К1-1	П4 мойка кухонная	Ø50	400	ст. В: 3925 от лев. угла

Ведомость привязок (продолжение)

Код	Прибор	Ø	Н, мм	Привязка, мм
В1-2	П6** стиральная машина	½"	600	ст. В: 2115 от лев. угла
К1-2	П6** стиральная машина	Ø40	600	ст. В: 2315 от лев. угла

Условные обозначения

- вывод В1 (код — в ведомости привязок)
- вывод Т3 (код — в ведомости привязок)
- вывод К1 (код — в ведомости привязок)
- сантехприбор по расстановке (габарит модели)
- дверной проём; окно — сплошной контур

Примечания

1. Габариты и высоты приборов, межосевые смесителей и места кранов — по паспортам выбранных приборов, сверяются до разметки стен.
2. Высоты Н — от чистого пола помещения, мм; отметка чистого пола и потолка — у левого края вида (от ±0,000 объекта). Привязки — от левого чистового угла вида (облицовка стен вычтена), как на развёртках стен.
3. Ревизионные люки к арматуре и ревизиям в данных не заданы: место и размер не определены (записи реестра нет).
4. Мойка, ПММ и фильтр — выводы в шкафу мойки; диаметры и положение сифона и кранов сверить по паспортам приборов и чертежам модуля.
5. Часть подписей выводов не уместилась у знака: коды и высоты — в ведомости привязок.
6. Расчёт систем водоснабжения и канализации и подбор оборудования выполняет проектная организация; лист задаёт места и высоты выводов.

1000 мм · печать 1:1

Изм.	Кол.уч	Лист	№ док.	Подп.	Дата
Разраб.		Кырлан А.С.			04.11.26
Пров.					
ГИП					
Н. контр.					
Утв.					

ГД-2026-006-АИ

Квартира 58 м²

Общая площадь 55,23* м² · * размеры приняты, не замерены (реестр — л. 6, 7, К-5)

Дизайн-проект интерьера

Стадия	Лист	Листов
РП	34	87

Развёртки мокрых зон: выводы ВК. Кухня-гостиная

М 1:20

Кырлан Александр Сергеевич


выпуск 04.11.2026 № 94e5be632e · стр. 39 из 96

Развёртки мокрых зон: выводы ВК. Ванная (лист 1 из 2)


ПРЕДВАРИТЕЛЬНО · не для производства работ · открыто пунктов: 10 (реестр — л. 6, 7)

пом. 3 · выводы В1, Т3, К1 на стенах · высоты от чистого пола, привязки от чистовых углов, мм


Стена А (М 1:20)

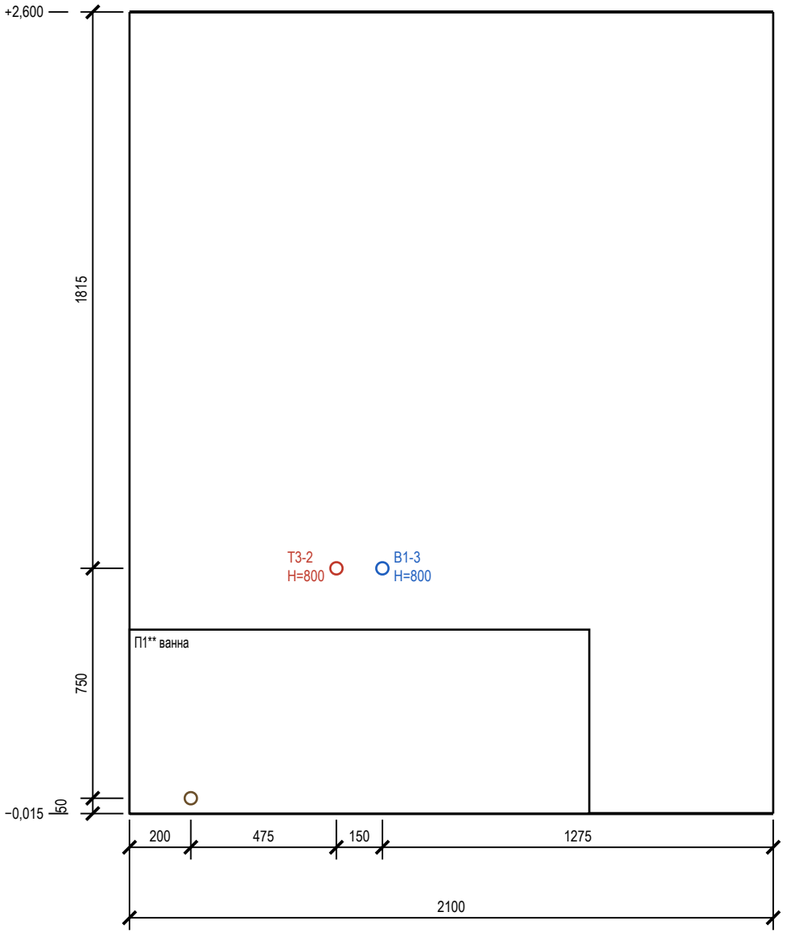

Стена Б (М 1:20)

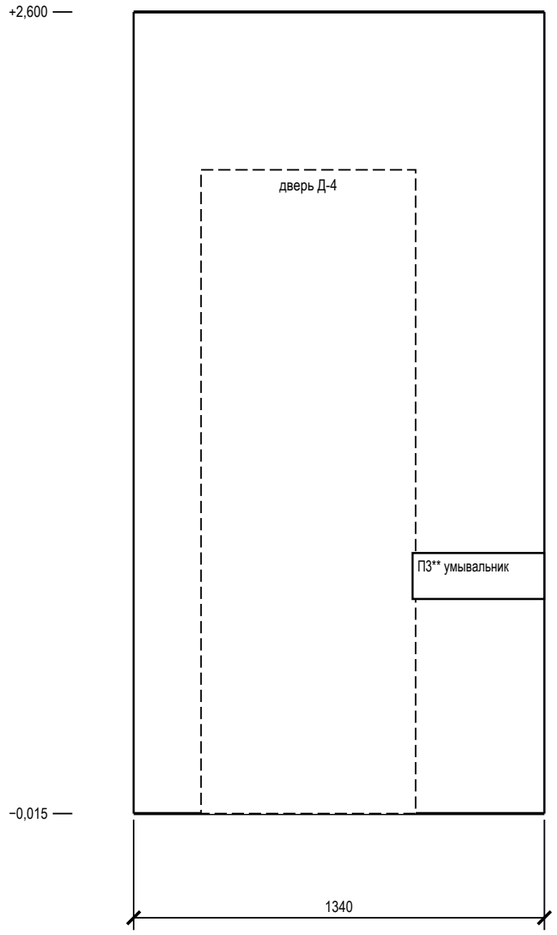

Стена В (М 1:20)

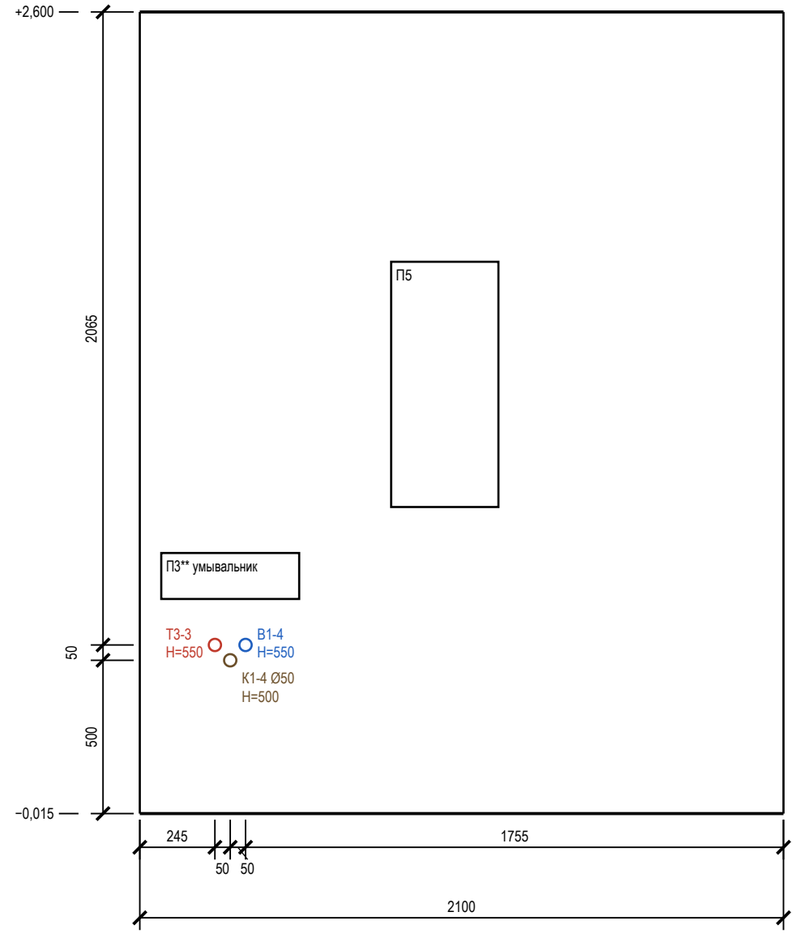

Ведомость привязок выводов (от чистого пола и угла)

Код	Прибор	Ø	Н, мм	Привязка, мм
В1-3	П1** ванна	½"	800	ст. А: 825 от лев. угла
Т3-2	П1** ванна	½"	800	ст. А: 675 от лев. угла
К1-3	П1** ванна	Ø50	50	ст. А: 200 от лев. угла

Ведомость привязок (продолжение)

Код	Прибор	Ø	Н, мм	Привязка, мм
В1-4	П3** умывальник	½"	550	ст. В: 345 от лев. угла
Т3-3	П3** умывальник	½"	550	ст. В: 245 от лев. угла
К1-4	П3** умывальник	Ø50	500	ст. В: 295 от лев. угла

Условные обозначения

- вывод В1 (код — в ведомости привязок)
- вывод Т3 (код — в ведомости привязок)
- вывод К1 (код — в ведомости привязок)
- сантехприбор по расстановке (габарит модели)
- дверной проём; окно — сплошной контур

Допущения и предложения на листе. Основа листа: размеры сняты с плана заказчика, контрольный обмер не выполнен (К-5); высота потолка 2700 мм принята: на плане заказчика не указана (К-5); подрайон климата не задан — принят не северный (жилые от 2,5 м) (К-4); толщины стен приняты: наружные 250 мм, перегородки 120 мм — не обмерены (К-5); разрешённая мощность 15 кВт принята по типовой квартире, технических условий нет (К-6). Знак «**» — предложено, не утверждено (согласовать): К-2: П1, П3. См. лист открытых вопросов (лист 6, записи К-2, К-4–К-6).

Примечания

1. Габариты и высоты приборов, межосевые смесителей и места кранов — по паспортам выбранных приборов, сверяются до разметки стен.
2. Высоты Н — от чистого пола помещения, мм; отметка чистого пола и потолка — у левого края вида (от ±0,000 объекта). Привязки — от левого чистового угла вида (облицовка стен вычтена), как на развёртках стен.
3. Стояки в помещении: Ст К1-1 Ø110, Ст В1-1 Ø32, Ст Т3-1 Ø32 — положение на плане выводов; выводы подключаются к ним по схеме разводки.
4. Ревизионные люки к арматуре и ревизиям в данных не заданы: место и размер не определены (записи реестра нет).
5. Часть подписей выводов не уместилась у знака: коды и высоты — в ведомости привязок.
6. Помещение «Ванная» — 2 листа: стены 1) А, Б, В; 2) Г.
7. Расчёт систем водоснабжения и канализации и подбор оборудования выполняет проектная организация; лист задаёт места и высоты выводов.

1000 мм · печать 1:1

Изм.	Кол.уч	Лист	№ док.	Подп.	Дата
Разраб.		Кырлан А.С.			04.11.26
Пров.					
ГИП					
Н. контр.					
Утв.					

ГД-2026-006-АИ

Квартира 58 м²

Общая площадь 55,23* м² · * размеры приняты, не замерены (реестр — л. 6, 7, К-5)

Дизайн-проект интерьера

Стадия	Лист	Листов
РП	35	87

Развёртки мокрых зон: выводы ВК. Ванная (лист 1 из 2)

М 1:20

Кырлан Александр Сергеевич


выпуск 04.11.2026 № 94e55e632e · стр. 40 из 96

Развёртки мокрых зон: выводы ВК. Ванная (лист 2 из 2)

ПРЕДВАРИТЕЛЬНО · не для производства работ · открыто пунктов: 10 (реестр — л. 6, 7)

пом. 3 · выводы В1, Т3, К1 на стенах · высоты от чистого пола, привязки от чистовых углов, мм

Стена Г (М 1:20)

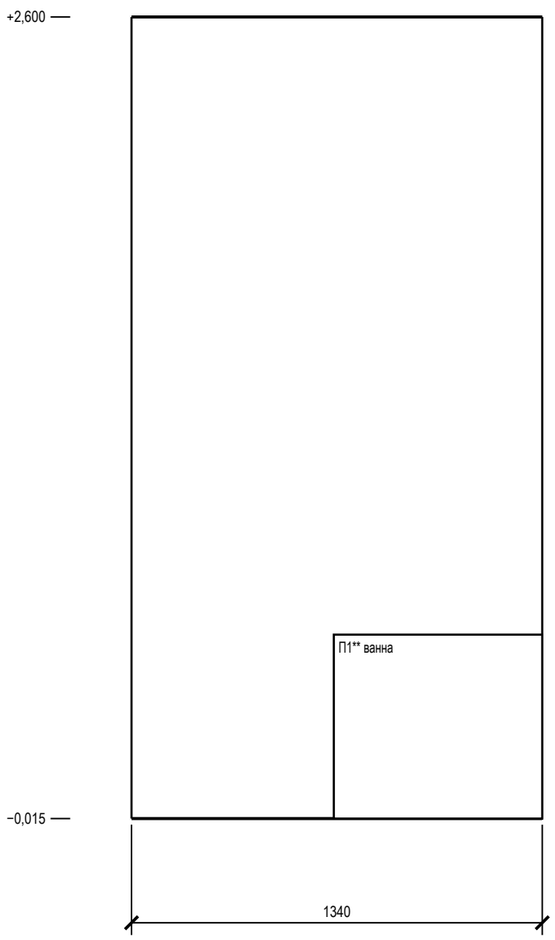

Ведомость привязок выводов (от чистого пола и угла)

Код	Прибор	Ø	H, мм	Привязка, мм
	выводов на стене нет			

Допущения и предложения на листе

Основа листа: размеры сняты с плана заказчика, контрольный обмер не выполнен (К-5); высота потолка 2700 мм принята: на плане заказчика не указана (К-5); подрайон климата не задан — принят не северный (жилые от 2,5 м) (К-4); толщины стен приняты: наружные 250 мм, перегородки 120 мм — не обмерены (К-5); разрешённая мощность 15 кВт принята по типовой квартире, технических условий нет (К-6).

Знак «**» — предложение проектировщика, заказчиком не утверждено (согласовать с заказчиком): К-2: П1 — ванна 1500 вместо 1600 — не заходит в проход перед проёмом Д-4; перед ванной 680 мм — глубина помещения.

См. лист открытых вопросов (лист 6, записи К-2, К-4–К-6).

Условные обозначения

- вывод В1 (код — в ведомости привязок)
- вывод Т3 (код — в ведомости привязок)
- вывод К1 (код — в ведомости привязок)
- сантехприбор по расстановке (габарит модели)
- дверной проём; окно — сплошной контур

Примечания

1. Габариты и высоты приборов, межосевые смесителей и места кранов — по паспортам выбранных приборов, сверяются до разметки стен.
2. Высоты Н — от чистого пола помещения, мм; отметка чистого пола и потолка — у левого края вида (от ±0,000 объекта). Привязки — от левого чистового угла вида (облицовка стен вычтена), как на развёртках стен.
3. Стояки в помещении: Ст К1-1 Ø110, Ст В1-1 Ø32, Ст Т3-1 Ø32 — положение на плане выводов; выводы подключаются к ним по схеме разводки.
4. Ревизионные люки к арматуре и ревизиям в данных не заданы: место и размер не определены (записи реестра нет).
5. Помещение «Ванная» — 2 листа: стены 1) А, Б, В; 2) Г.
6. Расчёт систем водоснабжения и канализации и подбор оборудования выполняет проектная организация; лист задаёт места и высоты выводов.

1000 мм · печать 1:1

Изм.	Кол.уч	Лист	№ док.	Подп.	Дата
Разраб.		Кырлан А.С.			04.11.26
Пров.					
ГИП					
Н. контр.					
Утв.					

ГД-2026-006-АИ

Квартира 58 м²

Общая площадь 55,23* м² · * размеры приняты, не замерены (реестр — л. 6, 7, К-5)

Дизайн-проект интерьера

Стадия	Лист	Листов
РП	36	87

Развёртки мокрых зон: выводы ВК. Ванная (лист 2 из 2)

М 1:20

Кырлан Александр Сергеевич


выпуск 04.11.2026 № 94e55e632e · стр. 41 из 96

Развёртки мокрых зон: выводы ВК. Санузел

ПРЕДВАРИТЕЛЬНО · не для производства работ · открыто пунктов: 10 (реестр — л. 6, 7)

пом. 4 · выводы В1, Т3, К1 на стенах · высоты от чистого пола, привязки от чистовых углов, мм

Стена Г (М 1:20)

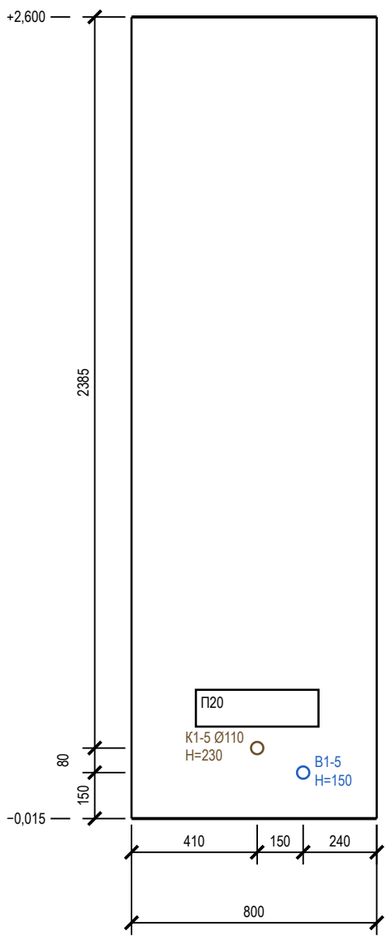

Ведомость привязок выводов (от чистого пола и угла)

Код	Прибор	Ø	H, мм	Привязка, мм
В1-5	П20 унитаз подвесной	½"	150	ст. Г: 560 от лев. угла
К1-5	П20 унитаз подвесной	Ø110	230	ст. Г: 410 от лев. угла

Условные обозначения

- вывод В1 (код — в ведомости привязок)
- вывод Т3 (код — в ведомости привязок)
- вывод К1 (код — в ведомости привязок)
- сантехприбор по расстановке (габарит модели)
- дверной проём; окно — сплошной контур

Примечания

1. Габариты и высоты приборов, межосевые смесителей и места кранов — по паспортам выбранных приборов, сверяются до разметки стен.
2. Высоты H — от чистого пола помещения, мм; отметка чистого пола и потолка — у левого края вида (от ±0,000 объекта). Привязки — от левого чистового угла вида (облицовка стен вычтена), как на развёртках стен.
3. Ревизионные люки к арматуре и ревизиям в данных не заданы: место и размер не определены (записи реестра нет).
4. Расчёт систем водоснабжения и канализации и подбор оборудования выполняет проектная организация; лист задаёт места и высоты выводов.

Допущения и предложения на листе

Основа листа: размеры сняты с плана заказчика, контрольный обмер не выполнен (К-5); высота потолка 2700 мм принята: на плане заказчика не указана (К-5); подрайон климата не задан — принят не северный (жилые от 2,5 м) (К-4); толщины стен приняты: наружные 250 мм, перегородки 120 мм — не обмерены (К-5); разрешённая мощность 15 кВт принята по типовой квартире, технических условий нет (К-6).

См. лист открытых вопросов (лист 6, записи К-4–К-6).

1000 мм · печать 1:1

Изм.	Кол.уч	Лист	№ док.	Подп.	Дата
Разраб.		Кырлан А.С.			04.11.26
Пров.					
ГИП					
Н. контр.					
Утв.					

ГД-2026-006-АИ

Квартира 58 м²

Общая площадь 55,23* м² · * размеры приняты, не замерены (реестр — л. 6, 7, К-5)

Дизайн-проект интерьера

Стадия	Лист	Листов
РП	37	87

Развёртки мокрых зон: выводы ВК. Санузел

М 1:20

Кырлан Александр Сергеевич

выпуск 04.11.2026 № 94e55e632e · стр. 42 из 96

Спецификация сантехнического оборудования

Форма 1 ГОСТ 21.110-2013 · ГД-2026-006-АИ-ВК.СО · приборы, арматура, трубопроводы

ПРЕДВАРИТЕЛЬНО · не для производства работ · открыто пунктов: 10 (реестр — л. 6, 7)

Поз.	Наименование и техническая характеристика	Тип, марка, обозначение документа	Код продукции	Поставщик	Ед. изм.	Кол.	Масса 1 ед., кг	Примечание
	Санитарные приборы							
1	Ванна встраиваемая акриловая 1500×700 мм, с каркасом, экраном и отверстием слив-перелив	акриловая 1500×700, смеситель настенный		выбор заказчика	шт	1		П1**
2	Унитаз подвесной безободковый, с сиденьем микролифт, крепёж и звукоизолирующая прокладка	Laufen Pro 8.2096.6.000.000.1		выбор заказчика	шт	1		П20
3	Инсталляция для подвесного унитаза: рама высотой 1120 мм, бачок, клавиша смыва (ось клавиши 1050 мм от чистого пола)	аналог		выбор заказчика	шт	1		П20; короб ГКЛВ
4	Умывальник подвесной 450×450 мм, с отверстием под смеситель и переливом	Laufen Pro S 8.1096.3.000.104.1		выбор заказчика	шт	1		П3**
5	Мойка кухонная 700×480 мм, с переливом	мойка врезная 700×480 в шкафу М5		с кухонной мебелью	шт	1		П4
6	Полотенцесушитель электрический, IP44, с терморегулятором	аналог		выбор заказчика	шт	1		П5
	Смесители, сифоны и арматура приборов							
7	Смеситель для ванны настенный однорычажный, межосевое 150 мм, с душевым набором (лейка, шланг, держатель)	аналог		выбор заказчика	шт	1		П1**
8	Смеситель для умывальника однорычажный, с донным клапаном	аналог		выбор заказчика	шт	1		П3**
9	Смеситель кухонный однорычажный, высокий излив	аналог		выбор заказчика	шт	1		П4
10	Обвязка ванны слив-перелив Ø40/50 с сифоном	аналог		выбор заказчика	шт	1		П1**
11	Сифон для умывальника бутылочный Ø32/40–50, с гофрой к выпуску	аналог		выбор заказчика	шт	1		П3**
12	Сифон для мойки Ø40/50	аналог		выбор заказчика	шт	1		П4
13	Сифон для стиральной машины встраиваемый в стену Ø50, с обратным клапаном	аналог		выбор заказчика	шт	1		П6**
14	Кран угловой ½"×½" с гибкой подводкой 40 см (умывальники, мойка)	аналог		выбор заказчика	шт	4		по 2 на прибор
15	Кран шаровой угловой ½"×¾" для подключения стиральной и посудомоечной машины	аналог		выбор заказчика	шт	1		П6**
	Трубопроводы							
16	Труба полипропиленовая PP-R PN20 Ø20×3,4 (В1)	ГОСТ 32415-2013		выбор заказчика	м	13,5	0,17	9,2 + 2,6 + 10 %
17	Труба PP-R, армированная стекловолокном, PN20 Ø20×2,8 (Т3)	ГОСТ 32415-2013		выбор заказчика	м	9,5	0,15	6,4 + 1,9 + 10 %
18	Труба канализационная ПП Ø40 (К1)	ГОСТ 32414-2013		выбор заказчика	м	2,5		1,7 + 0,6 + 10 %
19	Труба канализационная ПП Ø50 (К1)	ГОСТ 32414-2013		выбор заказчика	м	8		6,1 + 0,9 + 10 %
20	Труба канализационная ПП Ø110 (К1)	ГОСТ 32414-2013		выбор заказчика	м	1,5		0,8 + 0,2 + 10 %
	Фасонные части и выводы							
21	Отвод канализационный ПП 45° Ø40	ГОСТ 32414-2013		выбор заказчика	шт	2		2 шт. на поворот
22	Отвод канализационный ПП 45° Ø50	ГОСТ 32414-2013		выбор заказчика	шт	12		2 шт. на поворот
23	Отвод канализационный ПП 45° Ø110	ГОСТ 32414-2013		выбор заказчика	шт	6		2 шт. на поворот
24	Тройник канализационный ПП 45° (врезки ветвей)	ГОСТ 32414-2013		выбор заказчика	шт	4		
25	Ревизия канализационная ПП (после поворота трассы)	ГОСТ 32414-2013		выбор заказчика	шт	5		доступ сохранить
26	Фитинги PP-R Ø20: тройники, угольники 90° (ветви и повороты В1, Т3)	ГОСТ 32415-2013		выбор заказчика	шт	22		
27	Водорозетка PP-R Ø20×½" настенная, с креплением	ГОСТ 32415-2013		выбор заказчика	шт	8		коды — лист выводов
	Узлы ввода, люки, короба							
28	Кран шаровой латунный Ду15 PN16 (отключение ввода)	аналог		выбор заказчика	шт	2		Ст В1-1, Ст Т3-1
29	Фильтр сетчатый косой Ду15	аналог		выбор заказчика	шт	2		
30	Счётчик воды крыльчатый Ду15 (ХВ, ГВ), с поверкой	аналог		выбор заказчика	шт	2		пломба УК
31	Клапан обратный Ду15	аналог		выбор заказчика	шт	2		
32	Люк ревизионный нажимной под плитку 300×400 мм	аналог		выбор заказчика	шт	1		к стоякам и арматуре
33	Звукоизоляция стояка К1 в коробе: рулонный звукоизоляционный материал ≥ 10 мм, обмотка стояка на высоту этажа	аналог		выбор заказчика	м	2,7		Ст К1-1
34	Короб К1 над полом: профиль ПН/ПС, ГКЛВ 12,5 мм под плитку	аналог		выбор заказчика	м	1,6		сечение — лист разводки

Примечания

1. Форма 1 ГОСТ 21.110-2013, ширины граф изменены по п. 4.1. «Аналог» — аналог по характеристикам: модели внести до черновых работ, привязки выводов сверить по паспортам.
2. Бытовая техника не входит (показана арматура подключения), мойка — в комплекте кухни (марка — модуля кухни, как у столяра). Длины труб — трасса листа разводки + подъёмы + 10 %.
3. Стояк К1 в коробе — звукоизоляция стояка в коробе без жёсткого контакта короба с трубой.
4. Расчёт систем водоснабжения и канализации, диаметры магистралей и подбор оборудования выполняет проектная организация.

Допущения и предложения на листе

Основа листа: размеры сняты с плана заказчика, контрольный обмер не выполнен (К-5); высота потолка 2700 мм принята: на плане заказчика не указана (К-5); подрайон климата не задан — принят не северный (жилые от 2,5 м) (К-4); толщины стен приняты: наружные 250 мм, перегородки 120 мм — не обмерены (К-5); разрешённая мощность 15 кВт принята по типовой квартире, технических условий нет (К-6).

Знак «**» — предложение проектировщика, заказчиком не утверждено (согласовать с заказчиком): К-2: П1 — ванна 1500 вместо 1600 — не заходит в проход перед проёмом Д-4; перед ванной 680 мм — глубина помещения; П3 — умывальник у стены В справа от ванны — перед ним свободно 750 мм, до стены Б 90 мм; К-7: П6 — стиральная машина на кухне: в ванной и санузле места нет; подвод ХВС с шаровым краном, слив — встраиваемый сифон с обратным клапаном (водяной затвор), отдельная группа 6 щита с УЗО 30 мА.

См. лист открытых вопросов (лист 6, записи К-2, К-4–К-7).

Изм.	Кол.уч	Лист	№ док.	Подп.	Дата	ГД-2026-006-АИ			
						Квартира 58 м²			
						Общая площадь 55,23* м² · * размеры приняты, не замерены (реестр — л. 6, 7, К-5)			
Разраб.		Кырлан А.С.			04.11.26	Дизайн-проект интерьера	Стадия	Лист	Листов
Пров.							РП	38	87
ГИП									
Н. контр.						Спецификация сантехнического оборудования	Кырлан Александр Сергеевич		
Утв.						М б/м			

выпуск 04.11.2026 № 94e55e632e · стр. 43 из 96

Техническое задание на подбор светильников

ПРЕДВАРИТЕЛЬНО · не для производства работ · открыто пунктов: 10 (реестр — л. 6, 7)

Параметры для подбора: светильники, ленты и блоки питания, слои света · б/м

Параметры светильников для подбора

Поз.	Марки	Наименование	Установка	Кол.	P, Вт	Σ P, Вт	Ф, лм	Тц, К	Ra	Угол, °	IP	Дим.	Слой	Группа	Пом.
1	Св1**	Подвесной	подвес, низ H=1450	1	40	40	3600	3000	90	—	20	—	общий	L1	1
2	Св2**	Трековая система	на потолке	4	12	48	950	3000	90	—	20	—	общий	L5	1
3	Св3	Линейный настенный	под верхними шкафами, H=1400	1	14	14	1080	3000	90	—	20	—	рабочий	L6	1
4	Св4	Потолочный накладной	на потолке	1	36	36	3200	2700	90	—	20	—	общий	L2	2
5	Св5**	Трековая система	на потолке	2	12	24	900	2700	90	—	20	—	общий	L2	2
6	Св6, Св7	Настенный (бра)	на стене, H=1300	2	4	8	250	2700	90	—	20	—	рабочий	L8	2
7	Св8	Встраиваемый точечный	в ГКЛ, корпус ≤ 70 мм	1	9	9	700	3000	90	—	44	—	общий	L4	3
8	Св9**	Настенный (бра)	над зеркалом, H=1900	1	6	6	400	3000	90	—	44	—	рабочий	L4	3
9	Св10	Встраиваемый точечный	в ГКЛ, корпус ≤ 70 мм	1	6	6	500	3000	90	—	44	—	общий	L9	4
10	Св11, Св12	Встраиваемый точечный	в ГКЛ, корпус ≤ 70 мм	2	9	18	800	3000	90	—	20	—	общий	L3	5
11	Св16	Потолочный накладной	на потолке, засветка стены	1	10	10	900	3000	90	—	20	—	общий	L7	6
		Итого		**17 шт**		**219**									

Слои света по помещениям

Пом.	Помещение	Слои света — группы включения (марки — в спецификации)	Σ P, Вт
1	Кухня-гостиная	общий — L1, L5; рабочий — L6	102
2	Спальня	общий — L2; рабочий — L8	68
3	Ванная	общий — L4; рабочий — L4	15
4	Санузел	общий — L9	6
5	Прихожая	общий — L3	18
6	Гардеробная	общий — L7	10

LED-ленты, линейные светильники и блоки питания

Марка	Пом.	L, м	U, В	Вт/м	Σ P, Вт	БП	P БП, Вт	Загр., %	Питание	Доступ к БП
Св2**	1	1,2	24	—	48	БП1	100	62	встроенный ввод	H=2300
—	1	1,8	24	—	14	БП1	100	62	встроенный ввод	H=2300
Св5**	2	0,8	24	—	24	БП2	60	40	встроенный ввод	H=2300

Слои света

общий — равномерный свет помещения, по норме освещённости

рабочий — местный свет задачи: столешница, зеркало, чтение у кровати

Допущения и предложения на листе

Основа листа: размеры сняты с плана заказчика, контрольный обмер не выполнен (К-5); высота потолка 2700 мм принята: на плане заказчика не указана (К-5); подрайон климата не задан — принят не северный (жилые от 2,5 м) (К-4); толщины стен приняты: наружные 250 мм, перегородки 120 мм — не обмерены (К-5); разрешённая мощность 15 кВт принята по типовой квартире, технических условий нет (К-6).

Знак «**» — предложение проектировщика, заказчиком не утверждено (согласовать с заказчиком): Св2 — общий свет зоны гостиной над журнальным столом М21 (трек шёл вдоль края стола М3 по проходу); трековая система 4 × 950 лм: поток принят до нормы освещённости, модель и паспорт не выбраны; Св5 — трековая система 2 × 900 лм: светильник добавлен проектировщиком, поток принят до нормы освещённости, модель и паспорт не выбраны; Св1 — подвес висел над проходом без заданной высоты, а стол — без света над ним: подвес по оси стола М3; Св9 — свет у зеркала — над зеркалом у умывальника по его оси (свет на лицо, а не над сантехникой).

См. лист открытых вопросов (лист 6, записи К-4–К-6).

Примечания

1. Позиции и марки Св — те же, что на плане освещения (лист 21) и в ведомости светильников (лист 23); группы L — по плану выключателей (лист 22).
2. Модели светильников не выбраны: лист — техническое задание на подбор. Модель по строке таблицы: поток, Тц, Ra, угол, IP и регулировка яркости не хуже указанных, мощность не больше; встраиваемые — под глубину короба (графа «Установка»). IP 20 — сухие помещения. После выбора моделей (артикул, производитель) лист выпускается как «Спецификация светильников».
3. Мощность и поток в таблице — требования к подбору (поток не меньше, мощность не больше указанных); после выбора модели — по её паспорту, Σ P — установленная мощность освещения. Оценка освещённости — на плане освещения; это не светотехнический расчёт.

Изм.	Кол.уч	Лист	№ док.	Подп.	Дата
Разраб.		Кырлан А.С.			04.11.26
Пров.					
ГИП					
Н. контр.					
Утв.					

ГД-2026-006-АИ

Квартира 58 м²

Общая площадь 55,23* м² · * размеры приняты, не замерены (реестр — л. 6, 7, К-5)

Дизайн-проект интерьера

Стадия	Лист	Листов
РП	39	87

Техническое задание на подбор светильников

М б/м

Кырлан Александр Сергеевич

выпуск 04.11.2026 № 94e55e632e · стр. 44 из 96

06

Потолки и ГКЛ-конструкции

Кырлан Александр Сергеевич


выпуск 04.11.2026 · 94e55e632e · стр. 45 из 96

План потолков

Уровни и марки потолков, короба с подсветкой, ниши под шторы, люки, вырезы · отметки низа от ±0,000 чистого пола · размеры в мм

ПРЕДВАРИТЕЛЬНО · не для производства работ · открыто пунктов: 10 (реестр — л. 6, 7)

Допущения и предложения на листе. Основа листа: размеры сняты с плана заказчика, контрольный обмер не выполнен (К-5); высота потолка 2700 мм принята: на плане заказчика не указана (К-5); подрайон климата не задан — принят не северный (жилые от 2,5 м) (К-4); толщины стен приняты: наружные 250 мм, перегородки 120 мм — не обмерены (К-5); разрешённая мощность 15 кВт принята по типовой квартире, технических условий нет (К-6). См. лист открытых вопросов (лист 6, записи К-4–К-6); по листу — К-4.

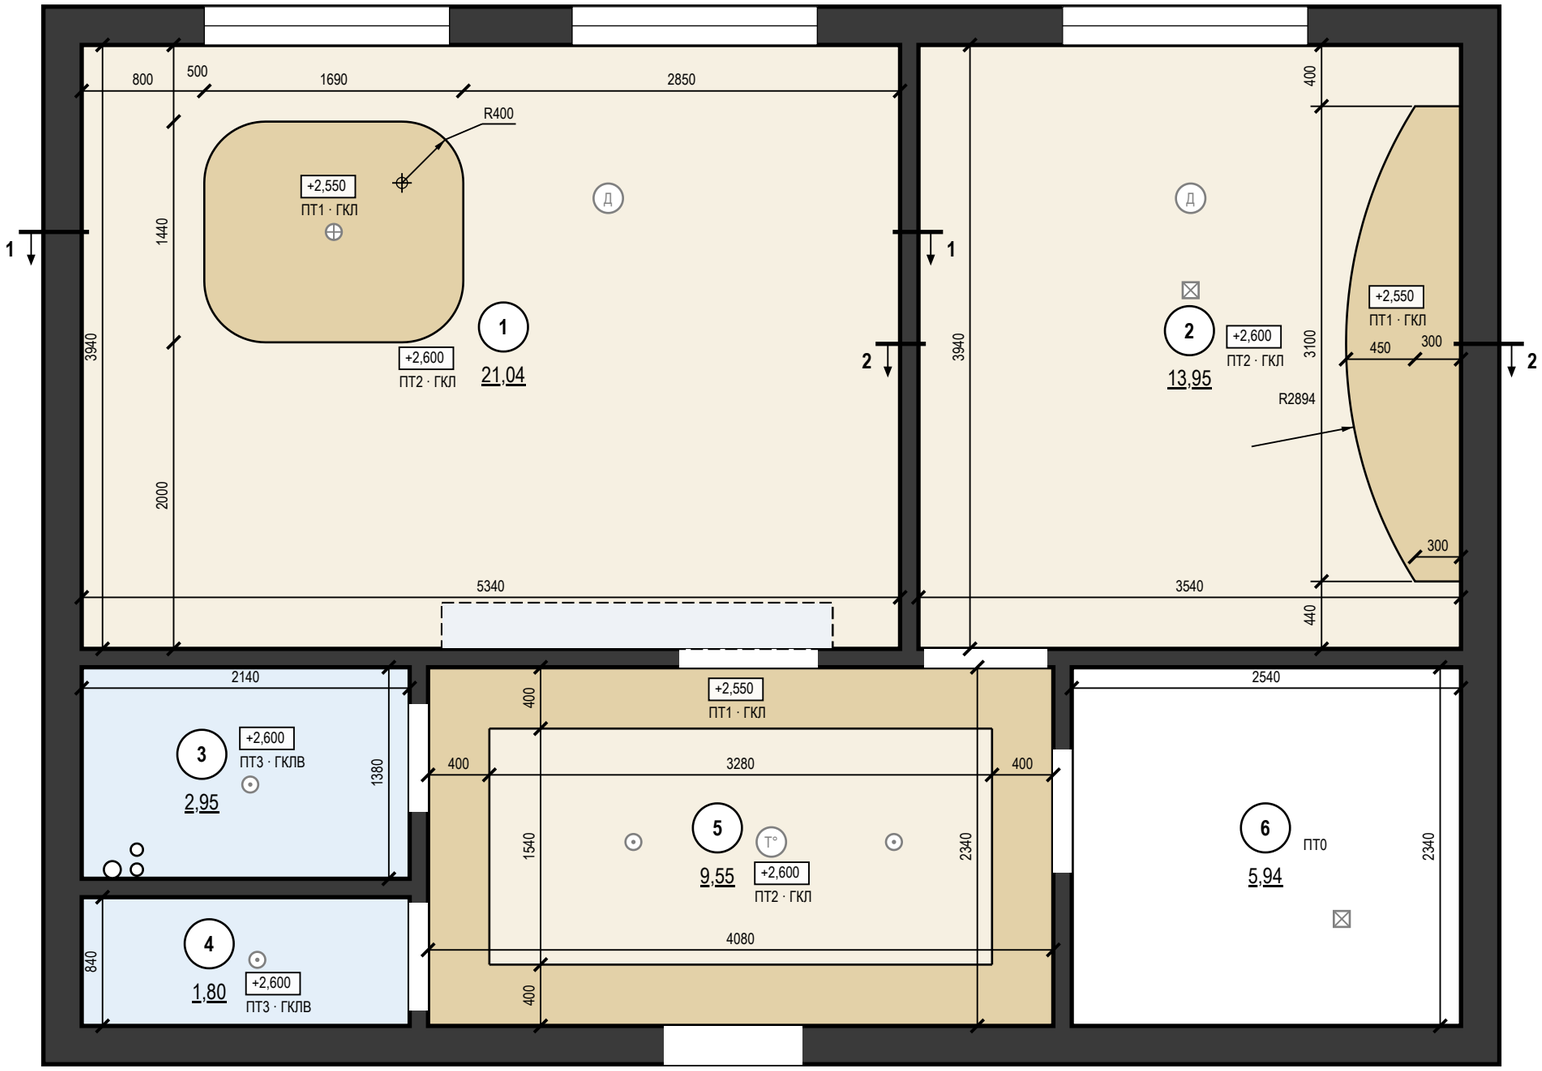

Ведомость потолков

Пом.	Марка	Конструкция	Низ / верх ниши	S, м²	Q
1	ПТ1	ГКЛ П113, остров	+2,550	2,30	Q3
1	ПТ2	ГКЛ П113	+2,600	18,74	Q3
2	ПТ1	ГКЛ П113, дуга	+2,550	1,88	Q3
2	ПТ2	ГКЛ П113	+2,600	12,07	Q3
3	ПТ3	ГКЛВ П113	+2,600	2,95	Q3
4	ПТ3	То же	+2,600	1,80	Q3
5	ПТ1	ГКЛ П113	+2,550	4,50	Q3
5	ПТ2	ГКЛ П113	+2,600	5,05	Q3
6	ПТ0	Существующий потолок, окраска	+2,700	5,94	
		Итого		**55,23**	

Ведомость вырезов и закладных в потолке

Марка	Устройство	Кол.	Пом.
	Светильник встраиваемый (марки — план освещения)	4	3, 4, 5
	Светильник накладной (марки — план освещения)	2	2, 6
	Светильник подвесной (марки — план освещения)	1	1
	Извещатель дымовой	2	1, 2
	Извещатель тепловой	1	5

Условные обозначения

- ПТ1 — ГКЛ по каркасу П113, низ +2,550
- ПТ2 — ГКЛ по каркасу П113, низ +2,600
- ПТ3 — ГКЛВ по каркасу П113, низ +2,600
- ПТ0 — существующий потолок, окраска, без подвесного потолка, низ +2,700
- граница уровней потолка (перепад)
- стояк: К1 — канализация, В1 — ХВС, Т3 — ГВС
- светильник подвесной — подложка с плана освещения
- светильник накладной — подложка с плана освещения
- светильник встраиваемый — подложка с плана освещения
- Д — извещатель дымовой на потолке — подложка
- T° — извещатель тепловой на потолке — подложка
- короб воздуховода вытяжки ГКЛ (трасса — план вентиляции)
- линия разреза у стен помещения, стрелка — направление взгляда
- +2,600 — отметка низа потолка, м (у ниши под шторы — верх ниши); под ней марка потолка
- 1 — номер помещения, площадь м²

Примечания

1. За отметку ±0,000 принят уровень чистого пола сухих помещений (готовое покрытие), а не существующего пола; пол пом. 3, 4 — −0,015; верх плиты перекрытия −0,064 — расчётный по пирогу пола, не замерен; существующий пол снимается до плиты, его отметка не замерена. Отметки в прямоугольниках — низ потолка; низ перекрытия +2,700. Марка потолка — одна конструкция и отметка на весь альбом.
2. Размеры помещений в свету (ширина × длина, мм), не поместившиеся на плане: пом. 4 — 2140 × 840.
3. Потолки ГКЛ — каркасная система П113: подвесы через 1000 (с запасом: СП 163, табл. 14 — до 1100 при 0,15 кН/м²), несущие профили через 500, основные через 1200 мм; листы — поперёк несущих профилей. В помещениях 3, 4 — ГКЛВ на оцинкованном каркасе.
4. Нижний уровень — пояс-короб по периметру шириной 400 мм, верхний — поле внутри пояса: пом. 5.
5. Примыкание к стенам: теневой шов 15 мм, техзазор 3 мм — пом. 1, 2, 5, по стенам, выровненным штукатуркой (узел 1); пом. 3, 4 — разделительная лента.
6. Светильники и потолочные устройства — подложка с планов освещения, слаботочных систем и вентиляции (положение — по ним); вырезы и закладные — по ведомости на листе, до обшивки; отверстия не совмещать с профилями, глубина корпуса светильника до 70 мм.
7. Разрезы 1–1, 2–2 — на листе 41; высоты мебели и дверных блоков сверены с низом потолка в разрезах; гибка бортов фигур и ленты ниш — там же; размеры фигурных уровней — фрагменты 1, 2 (лист 42).
8. Шпаклевание ГКЛ и условия приёмки — Q3: рассеянный дневной свет, осмотр с 2 м; боковой свет не оценивается.
9. Пом. 1: короб воздуховода кухонной вытяжки ГКЛ 300×200 мм (ширина от стены × высота), низ +2,500, длина 2,25 м — по трассе плана вентиляции, вдоль стен до входа в канал под воздуховод Ø125; каркас ПН 28×27 по стене и плите, ПП 60×27, лист ГКЛ 12,5.

1000 мм · печать 1:1

Изм.	Кол.уч	Лист	№ док.	Подп.	Дата
Разраб.		Кырлан А.С.			04.11.26
Пров.					
ГИП					
Н. контр.					
Утв.					

ГД-2026-006-АИ

Квартира 58 м²

Общая площадь 55,23* м² · * размеры приняты, не замерены (реестр — л. 6, 7, К-5)

Дизайн-проект интерьера

Стадия	Лист	Листов
РП	40	87

План потолков

М 1:40

Кырлан Александр Сергеевич


выпуск 04.11.2026 № 94e55e632e · стр. 46 из 96

Разрезы и узлы потолков

Разрезы по потолкам с отметками уровней · размеры в мм


Разрез 1–1 (М 1:40)

Пом. 1 Кухня-гостиная; линия разреза — план потолков, лист 40

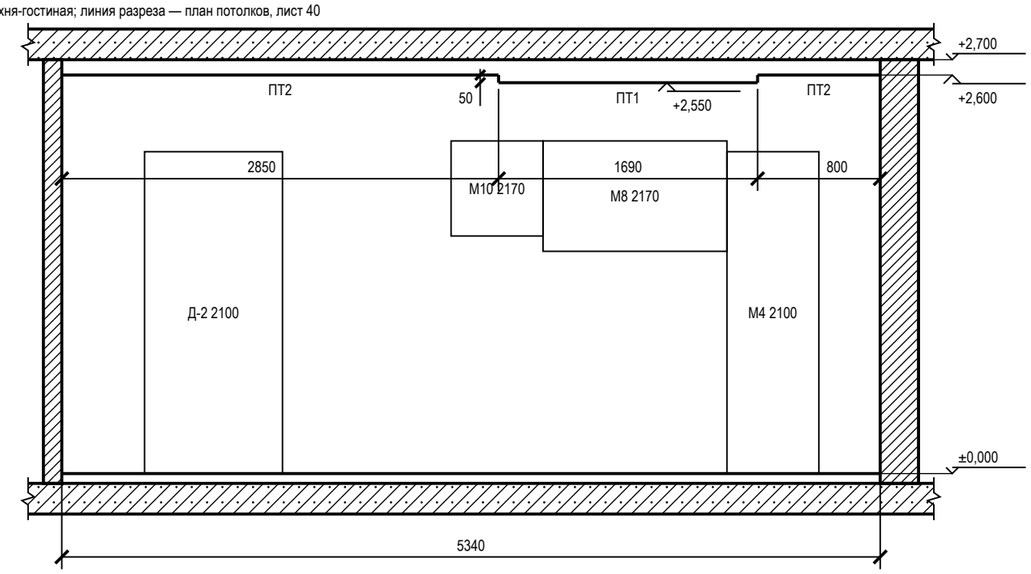

Разрез 2–2 (М 1:40)

Пом. 2 Спальня; линия разреза — план потолков, лист 40

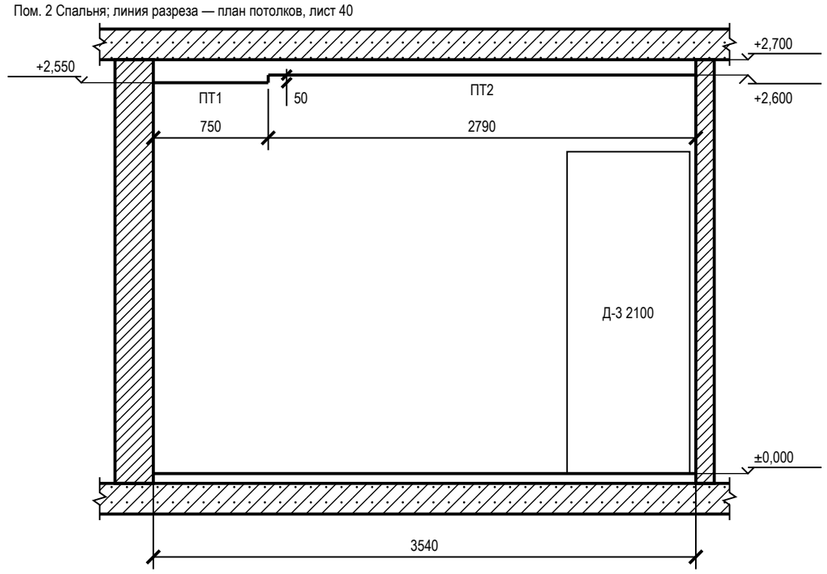

Условные обозначения

- плита перекрытия в сечении
- стена в сечении
- потолок ГКЛ в сечении; под линией — марка потолка (план потолков)
- мебель и дверные проёмы за секущей плоскостью; число — марка и верх от чистого пола, мм

Примечания

1. Разрезы — по линиям 1–1, 2–2 на плане потолков (лист 40). Отметки — от ±0,000 чистого пола, м; размеры — мм.
2. Высоты мебели и дверных блоков за секущей плоскостью сверены с низом потолка над ними: верх ниже низа короба и поля.
3. ГКЛ 12,5 мм по каркасу П113.
4. Толщины плит перекрытия и пирога пола показаны условно.
5. Ведомость объёмов потолков (лист ГКЛ, профиль, подвесы, лента, блоки питания, люки) — на листе 42.
6. Фрагменты 1, 2 — помещения с фигурными уровнями (размеры фигур, радиусы, отметки) — на листе 42.

1000 мм · печать 1:1

Допущения и предложения на листе

Основа листа: размеры сняты с плана заказчика, контрольный обмер не выполнен (К-5); высота потолка 2700 мм принята: на плане заказчика не указана (К-5); подрайон климата не задан — принят не северный (жилые от 2,5 м) (К-4); толщины стен приняты: наружные 250 мм, перегородки 120 мм — не обмерены (К-5); разрешённая мощность 15 кВт принята по типовой квартире, технических условий нет (К-6).
См. лист открытых вопросов (лист 6, записи К-4–К-6).

Изм.	Кол.уч	Лист	№ док.	Подп.	Дата
Разраб.		Кырлан А.С.			04.11.26
Пров.					
ГИП					
Н. контр.					
Утв.					

ГД-2026-006-АИ

Квартира 58 м²

Общая площадь 55,23* м² · * размеры приняты, не замерены (реестр — л. 6, 7, К-5)

Дизайн-проект интерьера

Стадия	Лист	Листов
РП	41	87

Разрезы и узлы потолков

М 1:40


Кырлан Александр Сергеевич

Разрезы и узлы потолков (продолжение)

Фрагменты фигурных уровней · ведомость объёмов · размеры в мм

Фрагмент 1. Пом. 1 Кухня-гостиная — уровни потолка (М 1:50)

Цепочки — от чистых граней стен; отметки — низ уровня от ±0,000

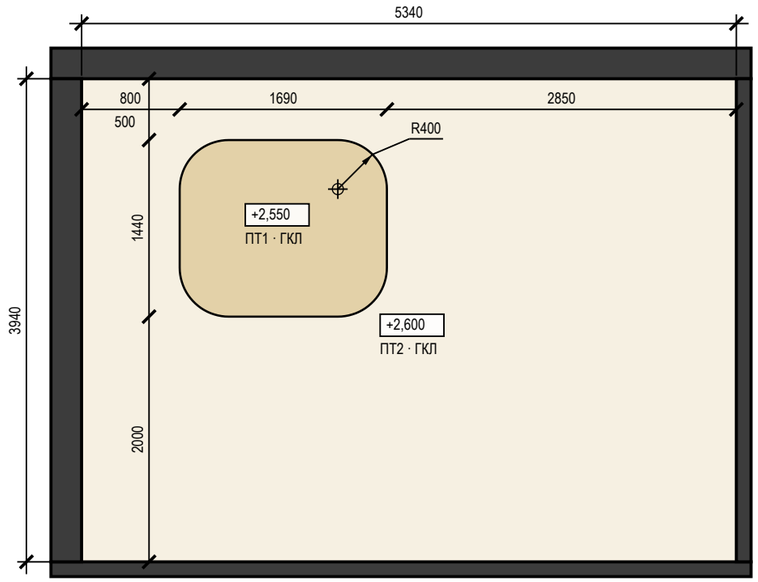


ПТ1 — низ +2,550

ПТ2 — низ +2,600

Фрагмент 2. Пом. 2 Спальня — уровни потолка (М 1:50)

Цепочки — от чистых граней стен; отметки — низ уровня от ±0,000

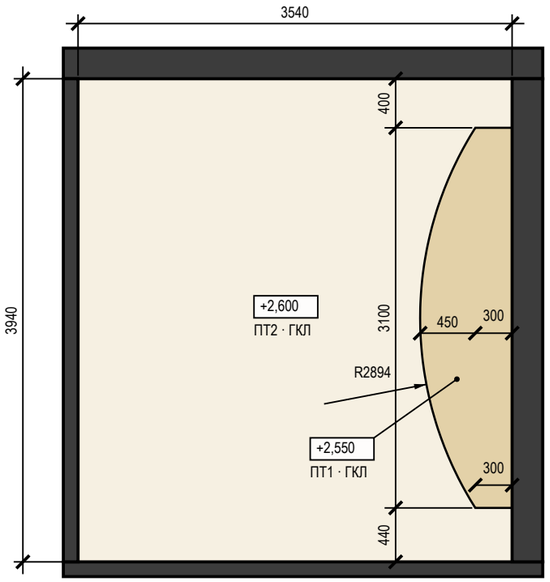

ПТ1 — низ +2,550

ПТ2 — низ +2,600

Ведомость объёмов потолков

Позиция	Ед.	Кол.	Пом.
Лист ГКЛ 12,5	м²	45,36	1, 2, 5
Лист ГКЛВ 12,5	м²	4,75	3, 4
Лист ГКЛ арочный 6,5	м²	0,25	1
Борта и карнизы (входят в площади листов выше)	м²	0,95	1, 2, 5
Профиль ПП 60×27	м	142,49	1, 2, 3, 4, 5
Профиль ПН 28×27	м	97,53	1, 2, 3, 4, 5
Подвес прямой	шт.	55	1, 2, 3, 4, 5
Анкер-клин к плите	шт.	55	1, 2, 3, 4, 5
Шуруп TN 3,5×25	шт.	1156	1, 2, 3, 4, 5
Лента армирующая для швов	м	60,29	1, 2, 3, 4, 5
Шпаклёвка для швов	кг	20,10	1, 2, 3, 4, 5
Грунтовка (швы)	л	5,02	1, 2, 3, 4, 5
Лента разделительная по периметру	м	59,36	1, 2, 3, 4, 5
Сплошная шпаклёвка и окраска (площадь развёртки)	м²	50,24	1, 2, 3, 4, 5

Допущения и предложения на листе

Основа листа: размеры сняты с плана заказчика, контрольный обмер не выполнен (К-5); высота потолка 2700 мм принята: на плане заказчика не указана (К-5); подрайон климата не задан — принят не северный (жилые от 2,5 м) (К-4); толщины стен приняты: наружные 250 мм, перегородки 120 мм — не обмерены (К-5); разрешённая мощность 15 кВт принята по типовой квартире, технических условий нет (К-6).

См. лист открытых вопросов (лист 6, записи К-4–К-6).

Примечания

1. ГКЛ 12,5 мм по каркасу П113; условные обозначения разрезов — на листе 41.
2. Фрагменты 1, 2 (план потолков — лист 40) — фигурные уровни потолка крупно: привязки краёв и центров фигур к чистым граням стен, радиусы (R) с центрами, хорда и стрелка дуги, отметки низа каждого уровня; цвета уровней — как на плане потолков.
3. Фигурные уровни: борт — ГКЛ по ПН с надрезами (на дуге шаг стоек борта 300 мм при R до 2500, 400 — до 5000) или по гнутому заводскому профилю (СП 163, 6.3.3); гибка: остров пом. 1 R400 — ГКЛ 6,5 мокрой гибкой; дуга пом. 2 R2894 — ГКЛ 12,5 сухой гибкой (СП 163, табл. 9).
4. Ведомость объёмов — по геометрии плана потолков: Лист ГКЛ 12,5 — плоскости уровней + борта (без арочных участков); Лист ГКЛВ 12,5 — плоскости уровней + борта; Лист ГКЛ арочный 6,5 — кривая борта × высота борта и стенки ниши × 2 слоя (R400 мокрая гибка); Борта и карнизы — длина перепада × перепад; Профиль ПП 60×27 — S × (1/шаг несущ. + 1/шаг осн.) + стойки бортов; Профиль ПН 28×27 — периметр стен + 2 × перепады + карнизы; Подвес прямой — по раскладке: S уровня / (шаг осн. × шаг подвесов), пояс уже шага — ряд вдоль пояса, фигура — по контуру; шаг подвесов — не больше табл. 14 СП 163; Анкер-клин к плите — по одному на подвес (Knauf П113); Шуруп TN 3,5×25 — 23 шт./м² (Knauf П113, табл. 2 альбома П 11); Лента армирующая для швов — 1,2 м/м² листа (Knauf); Шпаклёвка для швов — 0,4 кг/м² листа, только швы (Knauf); Грунтовка (швы) — 0,1 л/м² листа, только швы (Knauf); Лента разделительная по периметру — периметр стен под потолком ГКЛ; Сплошная шпаклёвка и окраска (площадь развёртки) — плоскости + борта; расход — по паспорту материала (норма расхода на сплошной слой не подтверждена); без запаса на подрезку (при закупке листа: ×1,075 при S > 20 м², ×1,175 — 10–20 м², ×1,275 — < 10 м²).

1000 мм · печать 1:1

Изм.	Кол.уч	Лист	№ док.	Подп.	Дата
Разраб.		Кырлан А.С.			04.11.26
Пров.					
ГИП					
Н. контр.					
Утв.					

ГД-2026-006-АИ

Квартира 58 м²

Общая площадь 55,23* м² · * размеры приняты, не замерены (реестр — л. 6, 7, К-5)

Дизайн-проект интерьера

Стадия	Лист	Листов
РП	42	87

Разрезы и узлы потолков (продолжение)

М 1:50

Кырлан Александр Сергеевич


выпуск 04.11.2026 № 94e55e632e · стр. 48 из 96

Раскладка плитки. Планы полов


Раскладка от чистовых размеров · размеры в мм · отметки от ±0,000

ПРЕДВАРИТЕЛЬНО · не для производства работ · открыто пунктов: 10 (реестр — л. 6, 7)

Фрагмент 1. Ванная (пом. 3). Пол 600×600, шов 2 мм, М 1:20

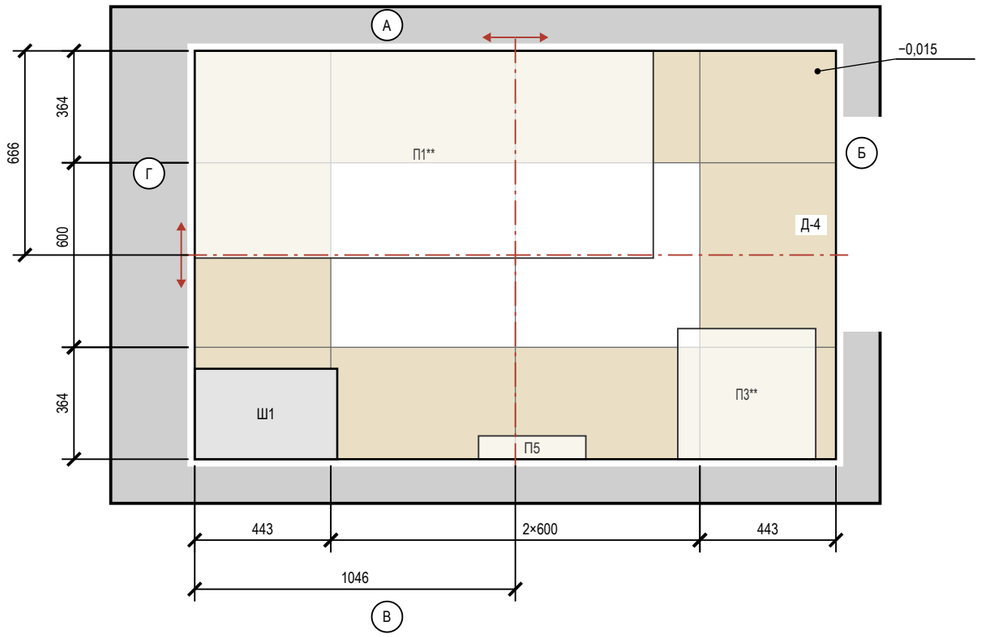

Фрагмент 2. Санузел (пом. 4). Пол 600×600, шов 2 мм, М 1:20

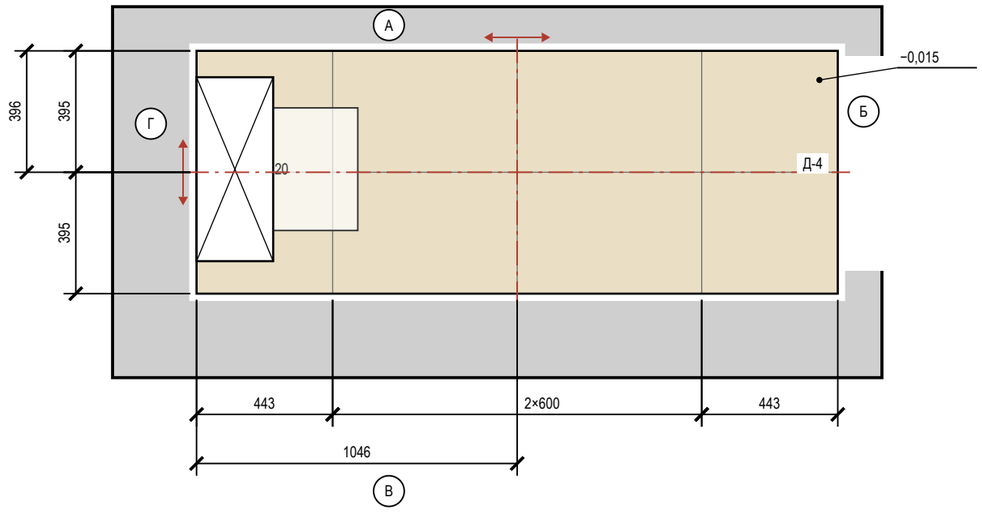

Ведомость материалов

Материал	Класс, код	Норма расхода	Кол-во
Затирка	класс не задан	(a+b)/ab·шов·t·1,6	3,9 кг
Клей	C2 S1	1,5 кг/м²·мм, слой 5	35 кг (2 меш.)
Клей	C2	1,5 кг/м²·мм, слой 5	332 кг (14 меш.)
Гидроизоляция	обмазочная, 2 слоя: пол, стены по периметру и зоны замачивания	по ТУ	13,4 м²
Демпф. лента	по периметру пола из плитки		21,0 м

Ведомость плитки

Помещение, поверхность	Плитка, код	Формат	Шов	S, м²	Целых	Подр.	С запасом
Ванная, пол	SG651622R	600×600	2	2,95	2	10	14
Ванная, стены А–Г	610015000370	1200×600	2	14,95	0	40	44
Ванная, короб стояков Ш1 489×319	610015000370	1200×600	2	1,99	0	10	12
Санузел, пол	SG651622R	600×600	2	1,80	0	8	9
Санузел, стены А–Г	610015000370	1200×600	2	13,40	0	30	34
Санузел, короб инсталляции	610015000370	1200×600	2	1,47	0	7	8
Прихожая, пол	SG651622R	600×600	2	9,55	10	18	31
Итого 600×600				14,30	12	36	54
Итого 600×1200				**31,80**	**0**	**87**	**98**

Условные обозначения

- плитка целая; тонкая линия — шов
- плитка с подрезкой (размер — на цепочке)
- ось старта; стрелки — направление укладки
- сантехприбор: габарит, высота по практике
- короб инсталляции: плитка пола — до короба
- короб стояков (Ш…): плитка пола — до короба
- отметка чистого пола на полке выноски, м
- (А) обозначение стены А–Г (как на развёртках)

1000 мм · печать 1:1

Примечания

1. Раскладка от чистовых размеров: стены санузлов теряют 10 + 5 + 9 = 24 мм на сторону (штукатурка, клей, плитка); подрезки чистые, без шва.
2. Старт — от центра помещения (штрихпунктир, стрелки направление укладки); размер старта — от чистовых стен Г и А.
3. Раскладка пола «Прихожая» — на листе «Раскладка плитки. Прихожая».
4. Калибр партии не задан — до укладки замерить (рабочий размер W, ГОСТ 13996-2019) и пересчитать подрезки.
5. Количество: целые по раскладке + по одной на подрезку, запас 10 %; один артикул — одна партия и тон. Исключены поддон, короб, проёмы и места за коробом; S — по чистым граням: стены нетто = зона облицовки по ведомости отделки − место за коробом инсталляции 2,71 м² (плитку за коробом не кладут), короб отдельной строкой.
6. Клей C2 S1; C2 (ГОСТ Р 56387-2018), затирка класс не задан; расход — по ТУ выбранной марки.
7. Гидроизоляция: пол и стены 200 мм от ЧП; над ванной — до 2000 и 300 мм за борт (пом. 3) (см. развёртки); акт скрытых работ, пролив 24 ч.
8. Отметка чистого пола −0,015, порог 15 мм; стык с соседним покрытием — по оси полотна двери.

Допущения и предложения на листе

Основа листа: размеры сняты с плана заказчика, контрольный обмер не выполнен (К-5); высота потолка 2700 мм принята: на плане заказчика не указана (К-5); подрайон климата не задан — принят не северный (жилые от 2,5 м) (К-4); толщины стен приняты: наружные 250 мм, перегородки 120 мм — не обмерены (К-5); разрешённая мощность 15 кВт принята по типовой квартире, технических условий нет (К-6).

Знак «**» — предложение проектировщика, заказчиком не утверждено (согласовать с заказчиком): К-2: П1 — ванна 1500 вместо 1600 — не заходит в проход перед проёмом Д-4; перед ванной 680 мм — глубина помещения; ПЗ — умывальник у стены В справа от ванны — перед ним свободно 750 мм, до стены Б 90 мм.

См. лист открытых вопросов (лист 6, записи К-2, К-4–К-6).

Изм.	Кол.уч	Лист	№ док.	Подп.	Дата
Разраб.		Кырлан А.С.			04.11.26
Пров.					
ГИП					
Н. контр.					
Утв.					

ГД-2026-006-АИ

Квартира 58 м²

Общая площадь 55,23* м² · * размеры приняты, не замерены (реестр — л. 6, 7, К-5)

Дизайн-проект интерьера

Стадия	Лист	Листов
РП	43	87

Раскладка плитки. Планы полов

М 1:20

Кырлан Александр Сергеевич


выпуск 04.11.2026 № 94e55e632e · стр. 49 из 96

Раскладка плитки. Прихожая

Раскладка от чистовых размеров · размеры в мм · высоты фартука от чистого пола

ПРЕДВАРИТЕЛЬНО · не для производства работ · открыто пунктов: 10 (реестр — л. 6, 7)

Фрагмент 1. Прихожая (пом. 5). Пол 600×600, шов 2 мм, М 1:20

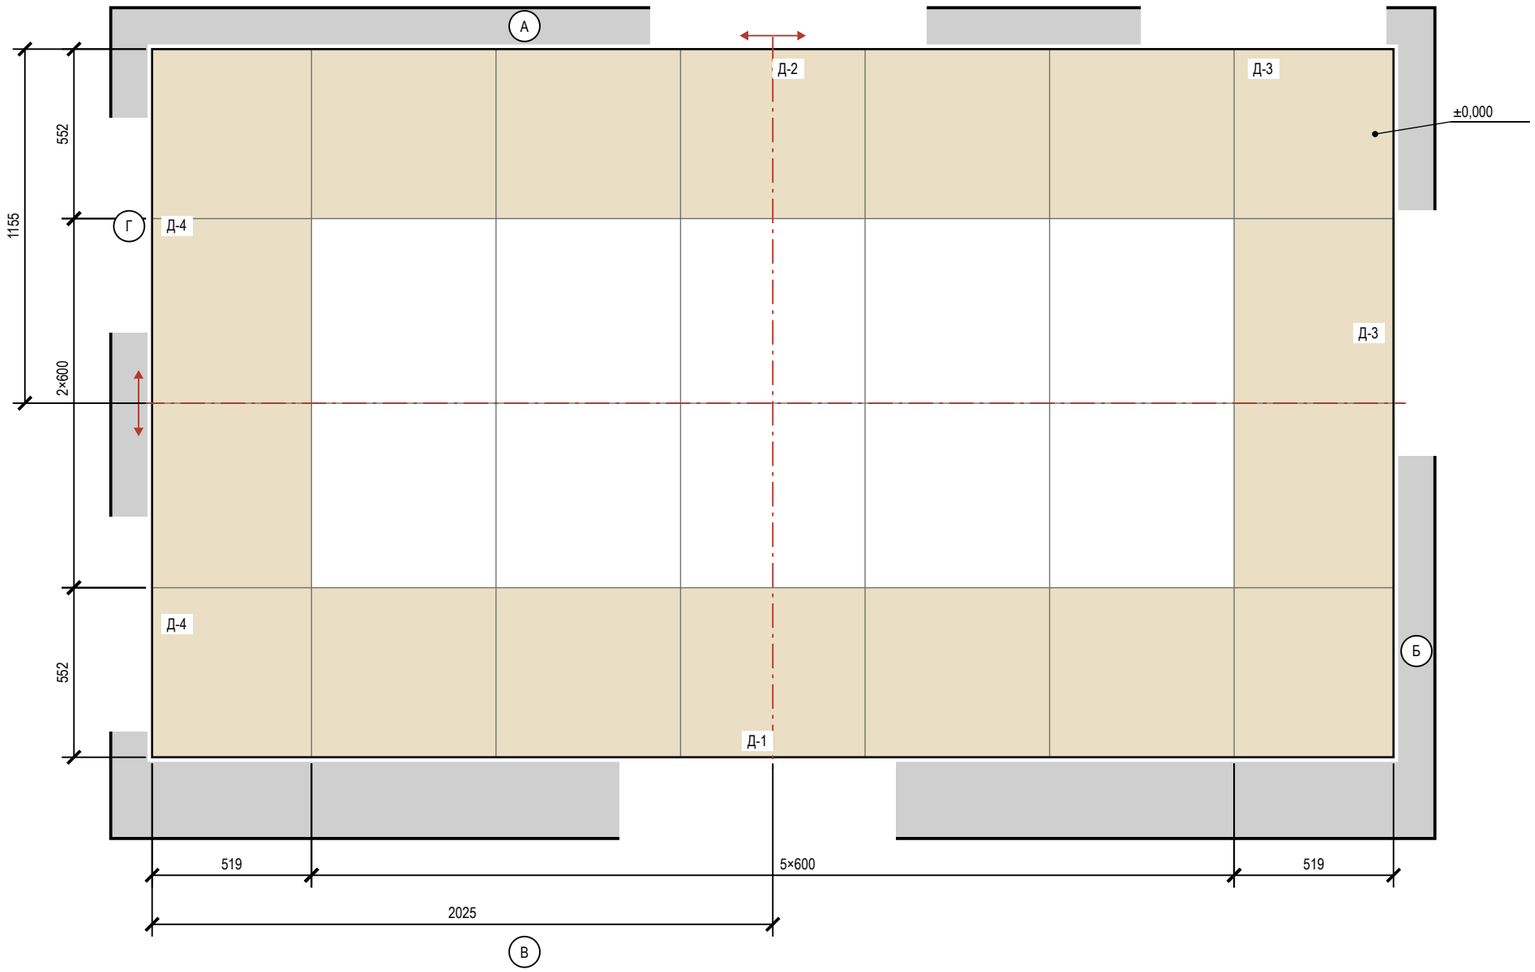

Условные обозначения

- плитка целая; тонкая линия — шов
- плитка с подрезкой (размер — на цепочке)
- ось старта; стрелки — направление укладки
- отметка чистого пола на полке выноски, м
- (А) обозначение стены А–Г (как на развёртках)

Подсчёт плитки

Поверхность	Формат	S, м²	Целых	Подр.	С запасом
Прихожая, пол	600×600	9,55	10	18	31

Примечания

1. Прихожая: керамогранит 600×600, длинная сторона — вдоль стен Б и Г, шов 2 мм, прямая раскладка от центра. Стены окрашены: раскладка от чистового контура минус штукатурка и шпаклёвка 15 мм на сторону (принято); подрезки 519 / 552 мм, срез — под плинтус.
2. Прихожая: деформационный зазор по периметру 8–10 мм под плинтусом; в проёмах — стык с соседним покрытием по оси полотна двери. Клей С2, затирка класс не задан.
3. Клей, затирка и итог по форматам — в ведомостях листа «Раскладка плитки. Планы полов».

Допущения и предложения на листе

Основа листа: размеры сняты с плана заказчика, контрольный обмер не выполнен (К-5); высота потолка 2700 мм принята: на плане заказчика не указана (К-5); подрайон климата не задан — принят не северный (жилые от 2,5 м) (К-4); толщины стен приняты: наружные 250 мм, перегородки 120 мм — не обмерены (К-5); разрешённая мощность 15 кВт принята по типовой квартире, технических условий нет (К-6).

См. лист открытых вопросов (лист 6, записи К-4–К-6).

1000 мм · печать 1:1

Изм.	Кол.уч	Лист	№ док.	Подп.	Дата
Разраб.		Кырлан А.С.			04.11.26
Пров.					
ГИП					
Н. контр.					
Утв.					

ГД-2026-006-АИ

Квартира 58 м²

Общая площадь 55,23* м² · * размеры приняты, не замерены (реестр — л. 6, 7, К-5)

Дизайн-проект интерьера

Стадия	Лист	Листов
РП	44	87

Раскладка плитки. Прихожая


М 1:20

Кырлан Александр Сергеевич

Раскладка плитки. Ванная. Развёртки стен

ПРЕДВАРИТЕЛЬНО · не для производства работ · открыто пунктов: 10 (реестр — л. 6, 7)

Пом. 3 · вид изнутри помещения · размеры в мм · высоты от чистого пола, отметки от ±0,000

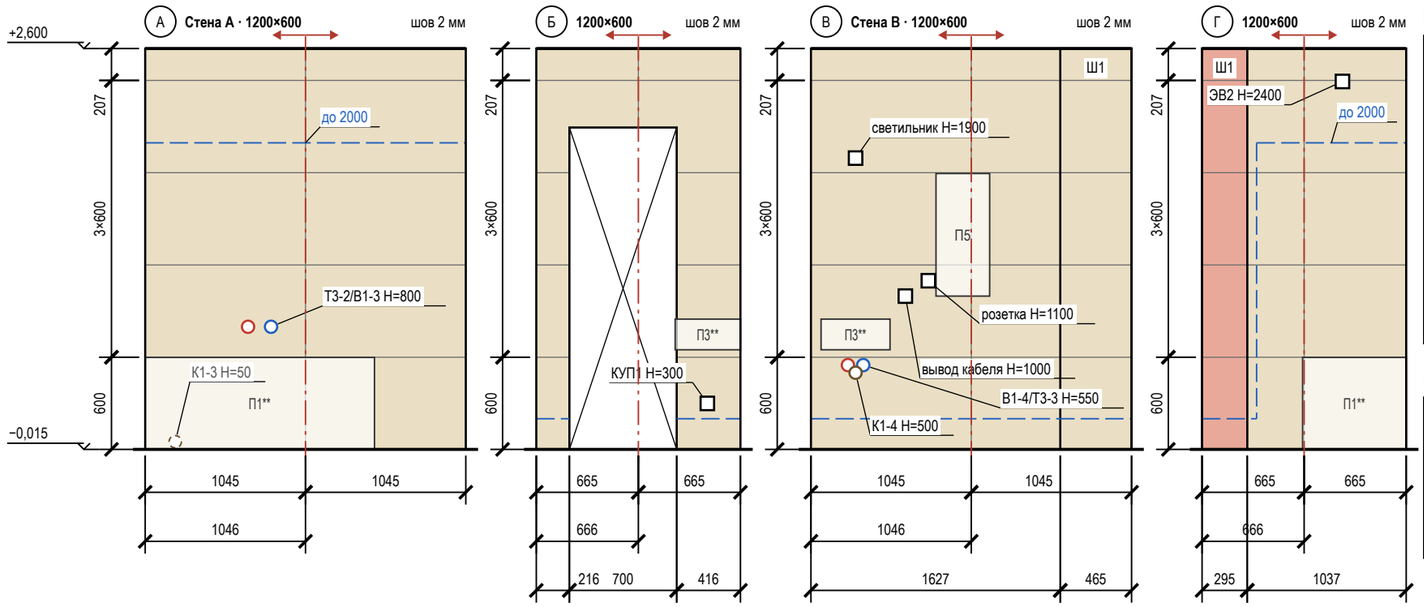

Подсчёт плитки по стенам и коробу

Поверхность	L × H, мм	S, м²	Целых	Подр.	С запасом	Подрезки: край / верх, мм
стена А	2092 × 2615	5,60	0	10	11	1045 / 1045; 207
стена Б	1332 × 2615	2,14	0	10	11	665 / 665; 207
стена В	2092 × 2615	4,38	0	10	11	1045 / 1045; 207
Ш1 489×319, ст. В	465 × 2615	1,22	0	5	6	лицо 465
стена Г	1332 × 2615	2,84	0	10	11	665 / 665; 207
Ш1 489×319, ст. Г	295 × 2615	0,77	0	5	6	лицо 295
Итого		**16,94**	**0**	**50**	**56**	

Сдвиг точек под раскладку

Точка (ВК, ЭОМ)	Стена	Проект: от угла / Н	Под раскладку: от угла / Н	Сдвиг, мм
розетка	В	766 / 1100	766 / 1203	Н +103
вывод кабеля	В	616 / 1000	616 / 902	Н −98
светильник	В	291 / 1900	291 / 1805	Н −95

Условные обозначения

- плитка целая; тонкая линия — шов
- плитка с подрезкой (размер — на цепочке)
- ось старта; стрелки — направление укладки
- верх гидроизоляции: 200 от ЧП, в мокрой зоне — «до …»
- проём — не облицовывается
- сантехприбор: габарит, высота по практике
- грань короба стояков (Ш…): своя сетка, за коробом плитку не кладут
- вывод В1 (код — в ведомости привязок)
- вывод Т3 (код — в ведомости привязок)
- вывод К1 (код — в ведомости привязок)
- вывод за прибором / в коробе (не на сетке)
- электроточка: марка и Н — по листам ЭОМ
- отметка уровня, м: ±0,000 — чистый пол жилых помещений
- низ потолка; серая полоса — стена без плитки
- (А) обозначение стены А–Г (как на развёртках)

Примечания

1. Вид изнутри, стены по часовой стрелке А → Г. Высоты — от чистого пола (−0,015), отметки — от ±0,000. Раскладка от чистовых размеров (штукатурка 10 + клей 5 + плитка 9 мм), подрезки чистые; старт — от оси стены, ряды от пола целыми.
2. Облицовка до потолка (+2,600).
3. Точки из таблицы сдвигов переносятся до черновой разводки (ЭОМ — по тем же числам).
4. Выводы ВК стоят по оси прибора и с прибором не двигаются — привязки по «Плану выводов сантехники» без сдвига; вне сетки (Т3-2/В1-3, В1-4/Т3-3, К1-4) отверстие в плитке коронкой по той же привязке, плитку не сдвигать.
5. Выводы — по «Плану выводов сантехники», электроточки — по ЭОМ, «*» — высота по практике; за приборами и в коробе (К1-3) — штриховым кольцом.
6. Гидроизоляция: 200 мм от ЧП по периметру; над ванной — до 2000 и 300 мм за борт (СП 29.13330.2011, п. 7.2 — на высоту замачивания); углы — лентой; акт скрытых работ, пролив.
7. Короб стояков Ш1: грани 465 мм (ст. В), 295 мм (ст. Г) — плиткой стен по рядам стены, целая плитка от наружного угла; угол — запил 45° или профиль; за коробом плитку не кладут. Люк 300×400 — на грани ст. В: высота — по месту ревизии стояка (положение стояков сверяется на объекте), кромки дверцы по швам сетки, дверца нажимная под плитку.

Допущения и предложения на листе

Основа листа: размеры сняты с плана заказчика, контрольный обмер не выполнен (К-5); высота потолка 2700 мм принята: на плане заказчика не указана (К-5); подрайон климата не задан — принят не северный (жилые от 2,5 м) (К-4); толщины стен приняты: наружные 250 мм, перегородки 120 мм — не обмерены (К-5); разрешённая мощность 15 кВт принята по типовой квартире, технических условий нет (К-6).

Знак «**» — предложение проектировщика, заказчиком не утверждено (согласовать с заказчиком): К-2: П1 — ванна 1500 вместо 1600 — не заходит в проход перед проёмом Д-4; перед ванной 680 мм — глубина помещения; П3 — умывальник у стены В справа от ванны — перед ним свободно 750 мм, до стены Б 90 мм.

См. лист открытых вопросов (лист 6, записи К-2, К-4–К-6).

1000 мм · печать 1:1

Изм.	Кол.уч	Лист	№ док.	Подп.	Дата
Разраб.		Кырлан А.С.			04.11.26
Пров.					
ГИП					
Н. контр.					
Утв.					

ГД-2026-006-АИ

Квартира 58 м²

Общая площадь 55,23* м² · * размеры приняты, не замерены (реестр — л. 6, 7, К-5)

Дизайн-проект интерьера

Стадия	Лист	Листов
РП	45	87

Раскладка плитки. Ванная. Развёртки стен


М 1:40

Кырлан Александр Сергеевич

Раскладка плитки. Санузел. Развёртки стен

ПРЕДВАРИТЕЛЬНО · не для производства работ · открыто пунктов: 10 (реестр — л. 6, 7)

Пом. 4 · вид изнутри помещения · размеры в мм · высоты от чистого пола, отметки от ±0,000

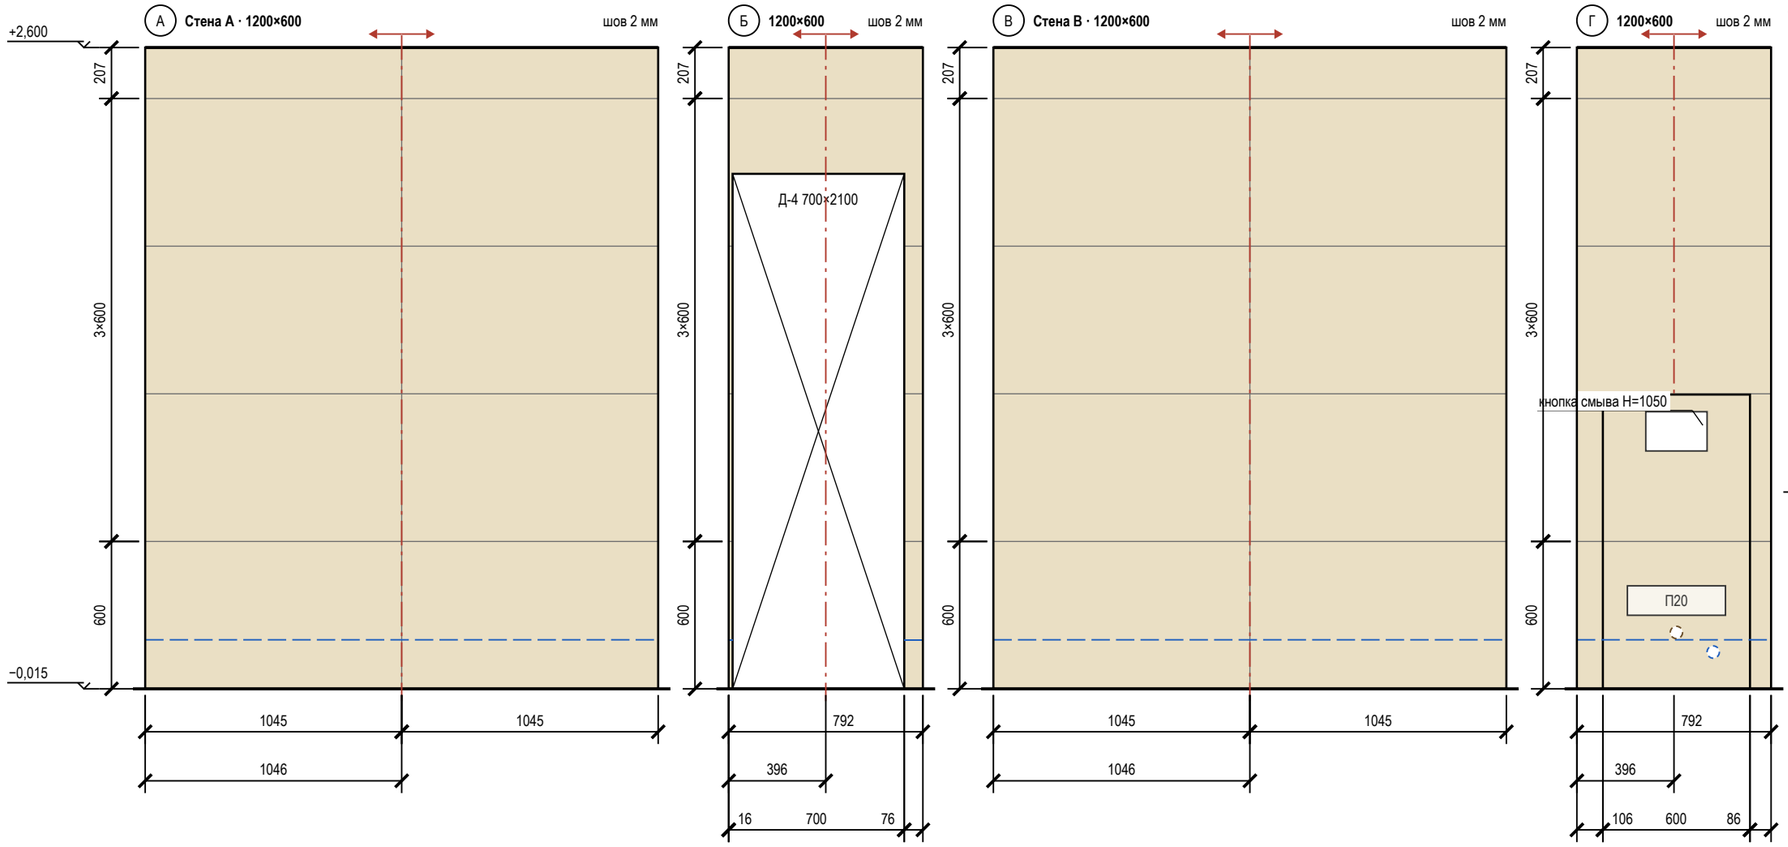

Условные обозначения

- плитка целая; тонкая линия — шов
- плитка с подрезкой (размер — на цепочке)
- ось старта; стрелки — направление укладки
- верх гидроизоляции: 200 от ЧП, в мокрой зоне — «до …»
- проём — не облицовывается
- сантехприбор: габарит, высота по практике
- короб инсталляции, в нём кнопка смыва 250×160
- вывод В1 (код — в ведомости привязок)
- вывод К1 (код — в ведомости привязок)
- вывод за прибором / в коробе (не на сетке)
- отметка уровня, м: ±0,000 — чистый пол жилых помещений
- низ потолка; серая полоса — стена без плитки
- А — обозначение стены А–Г (как на развёртках)

Подсчёт плитки по стенам и коробу

Поверхность	L × H, мм	S, м²	Целых	Подр.	С запасом	Подрезки: край / верх, мм
стена А	2092 × 2615	5,60	0	10	11	1045 / 1045; 207
стена Б	792 × 2615	0,73	0	5	6	792; 207
стена В	2092 × 2615	5,60	0	10	11	1045 / 1045; 207
стена Г	792 × 2615	1,48	0	5	6	792; 207
короб (ст. Г)	600×1200×250	1,47	0	7	8	лицо 600; бок. 250
Итого		**14,87**	**0**	**37**	**42**	

Примечания

1. Вид изнутри, стены по часовой стрелке А → Г. Высоты — от чистого пола (−0,015), отметки — от ±0,000. Раскладка от чистовых размеров (штукатурка 10 + клей 5 + плитка 9 мм), подрезки чистые; старт — от оси стены, ряды от пола целыми.
2. Облицовка до потолка (+2,600).
3. Открытые выводы и электроточки — на шве или в центре плитки (допуск 10 мм; плитка от 900 мм по высоте — на шве или не ближе 60 мм к нему).
4. Выводы — по «Плану выводов сантехники», электроточки — по ЭОМ, «*» — высота по практике; за приборами и в коробе (В1-5, К1-5) — штриховым кольцом.
5. Гидроизоляция: 200 мм от ЧП по периметру; углы — лентой; акт скрытых работ, пролив.
6. Короб 600×1200×250: лицо 600 мм от оси кнопки смыва, боковины, полка; углы — запил 45° или профиль; за коробом плитку не кладут.
7. Между коробом и углом полоса 86 и 106 мм — довести короб до угла.

Допущения и предложения на листе

Основа листа: размеры сняты с плана заказчика, контрольный обмер не выполнен (К-5); высота потолка 2700 мм принята: на плане заказчика не указана (К-5); подрайон климата не задан — принят не северный (жилые от 2,5 м) (К-4); толщины стен приняты: наружные 250 мм, перегородки 120 мм — не обмерены (К-5); разрешённая мощность 15 кВт принята по типовой квартире, технических условий нет (К-6).

См. лист открытых вопросов (лист 6, записи К-4–К-6).

1000 мм · печать 1:1

Изм.	Кол.уч	Лист	№ док.	Подп.	Дата
Разраб.		Кырлан А.С.			04.11.26
Пров.					
ГИП					
Н. контр.					
Утв.					

ГД-2026-006-АИ

Квартира 58 м²

Общая площадь 55,23* м² · * размеры приняты, не замерены (реестр — л. 6, 7, К-5)

Дизайн-проект интерьера

Стадия	Лист	Листов
РП	46	87

Раскладка плитки. Санузел. Развёртки стен

М 1:25

Кырлан Александр Сергеевич

выпуск 04.11.2026 № 94e55e632e · стр. 52 из 96

07

Полы и отделка

Кырлан Александр Сергеевич

выпуск 04.11.2026 № 94e55e632e · стр. 53 из 96

План полов

Покрытия, направление укладки, отметки чистого пола, стыки · размеры в мм · отметки в м


ПРЕДВАРИТЕЛЬНО · не для производства работ · открыто пунктов: 10 (реестр — л. 6, 7)

Условные обозначения

- тип 1 — инженерная доска, линии — вдоль доски
- тип 2 — керамогранит 600×600, сетка — формат плитки
- тип 3 — керамогранит 600×600, сетка — формат плитки
- номер типа пола (экспликация полов)
- схема пола, без масштаба: плита — штриховка, стяжка — точки, звукоизоляция — зигзаг, гидроизоляция — утолщённая линия с заведением на стену
- направление укладки (длинная сторона доски)
- отметка чистого пола, м
- стык в проёме: решение не задано
- стык в проёме: порог
- СТ1 — марка стыка (ведомость стыков)
- стояк: К1 — канализация, В1 ХВС, Т3 — ГВС
- 1 — номер помещения, площадь м²

Отметки по высоте

±0,000	чистый пол пом. 1, 2, 5, 6; отсчёт высот
−0,015	чистый пол пом. 3, 4, ниже на 15 мм
−0,064*	верх плиты — расчёт, не замер (задание на обмер)
сущ. пол	снимается до плиты; не замерен (задание на обмер)

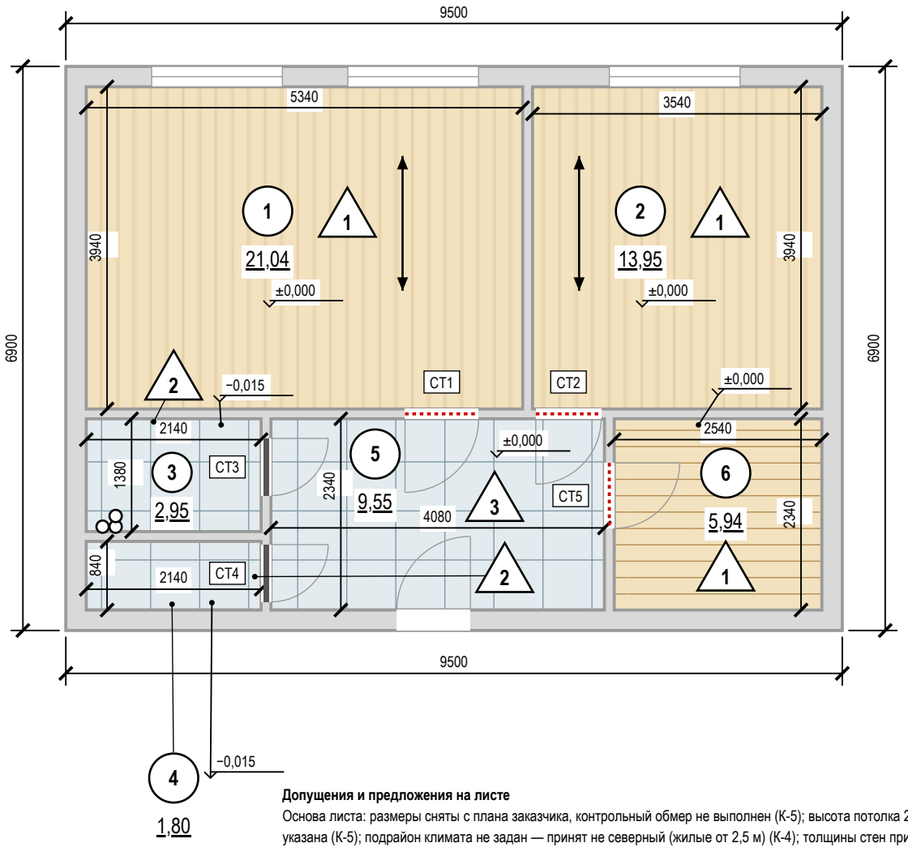




Допущения и предложения на листе

Основа листа: размеры сняты с плана заказчика, контрольный обмер не выполнен (К-5); высота потолка 2700 мм принята: на плане заказчика не указана (К-5); подрайон климата не задан — принят не северный (жилые от 2,5 м) (К-4); толщины стен приняты: наружные 250 мм, перегородки 120 мм — не обмерены (К-5); разрешённая мощность 15 кВт принята по типовой квартире, технических условий нет (К-6).

Знак «**» — предложение проектировщика, заказчиком не утверждено (согласовать с заказчиком): пол пом. 1, 2, 6 — артикул изделия не выбран: позиция описана характеристиками («аналог по характеристикам»), артикул выбирается при закупке.

См. лист открытых вопросов (лист 6, записи К-4–К-6).

Экспликация полов

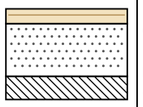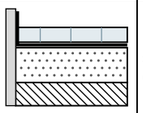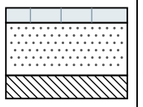Номер помещения	Тип пола	Схема пола	Данные элементов пола (наименование, толщина, основание), мм	Площадь, м²
1, 2, 6	1		Инженерная доска на клею — 14 Стяжка ЦПС М200 — 50 Плита перекрытия Всего 64 мм; ЧП ±0,000, верх плиты −0,064	40,93
3, 4	2		Керамогранит на клею С2 TE S1 — 14 Гидроизоляция обмазочная, 2 слоя, с заведением на стены 200 мм — 2 Стяжка ЦПС М200 — 33 Плита перекрытия Всего 49 мм; ЧП −0,015, верх плиты −0,064	4,75
5	3		Керамогранит на клею С2 TE S1 — 14 Стяжка ЦПС М200 — 50 Плита перекрытия Всего 64 мм; ЧП ±0,000, верх плиты −0,064	9,55
			Итого	**55,23**

Раскладка покрытий

Пом.	Укладка	Старт (оси от чистовых стен), мм	Отступ 1-го ряда / крайние плитки, мм
1	вдоль стен Б/Г, прямая	от стены Г, 1-й ряд вдоль неё	зазор от стены не задан
2	вдоль стен Б/Г, прямая	от стены Г, 1-й ряд вдоль неё	зазор от стены не задан
3	плитка	раскладка плиточника не задана	
4	плитка	раскладка плиточника не задана	
5	плитка	раскладка плиточника не задана	
6	вдоль стен А/В, прямая	от стены А, 1-й ряд вдоль неё	зазор от стены не задан

Стыки покрытий в проёмах

Марка	Проём	Типы пола	Отметки ЧП	Решение
СТ1	5–1 (Д-2)	3 / 1	±0,000 / ±0,000	не задано
СТ2	5–2 (Д-3)	3 / 1	±0,000 / ±0,000	не задано
СТ3	5–3 (Д-4)	3 / 2	±0,000 / −0,015	порог h=15 мм
СТ4	5–4 (Д-4)	3 / 2	±0,000 / −0,015	порог h=15 мм
СТ5	6–5 (Д-3)	1 / 3	±0,000 / ±0,000	не задано

Примечания

1. За отметку ±0,000 принят чистый пол, не существующий (блок отметок). Площади — по чистым размерам помещений, м²; размеры — в мм.
2. Стык разнотипных покрытий — по оси дверного полотна (под полотном в закрытом положении); решение стыка — по ведомости стыков.
3. Пол санузлов ниже смежных помещений на 15 мм за счёт меньшей толщины стяжки (верх плиты общий — по экспликации полов); гидроизоляция по стяжке с заведением на стены не менее 200 мм (СП 29.13330.2011, п. 7.2), до облицовки — тест проливом и акт скрытых работ.
4. Трубопроводы в конструкции пола не прокладываются: пирог пола 49–64 мм не вмещает выпуски канализации с уклоном — выпуски К1 ведутся по стенам над чистым полом в коробах (лист 30).
5. Звукоизоляционный слой под стяжкой проектом не предусмотрен (стяжка по плите): приведённый уровень ударного шума перекрытия с полом Lnw не более 60 дБ (СП 51.13330.2011, табл. 2) подтвердить по данным дома; при превышении — плавающая стяжка по звукоизоляции с демпферной лентой по контуру и у стояков, пирог пересчитать.
6. Штучные покрытия (инженерная доска): направление — по стрелке; влажность основания по СМ не более 2,0 % (по ТУ изготовителя).
7. Ровность основания — просвет под 2-метровой рейкой не более 2 мм: пом. 1, 2, 6 (инженерная доска), пом. 3, 4, 5 (керамогранит); проверить до укладки покрытия (СП 71.13330.2017, табл. 8.5).
8. Сетка на плитке — условная, в размер формата; точка старта и раскладка — по листу раскладки плитки.
9. Узор покрытия (заливка-код типа пола) прерывается под надписями — площадями помещений и отметками чистого пола.
10. Пироги полов — по экспликации полов: слои сверху вниз, толщины в мм; гидроизоляция мокрых зон — в пироге и в ведомости отделки; схема пола — без масштаба.

1000 мм · печать 1:1

Изм.	Кол.уч	Лист	№ док.	Подп.	Дата
Разраб.		Кырлан А.С.			04.11.26
Пров.					
ГИП					
Н. контр.					
Утв.					

ГД-2026-006-АИ

Квартира 58 м²

Общая площадь 55,23* м² · * размеры приняты, не замерены (реестр — л. 6, 7, К-5)

Дизайн-проект интерьера

Стадия	Лист	Листов
РП	47	87

План полов

М 1:75

Кырлан Александр Сергеевич

выпуск 04.11.2026 № 94e55e632e · стр. 54 из 96

Ведомость отделки помещений

Потолки, стены, низ стен, полы · площади в м², длины в м · отметки в м

Ведомость отделки помещений (форма 1 прил. А ГОСТ 21.501-2018)

№	Наименование помещения	Потолок			Стены и перегородки			Низ стен (плинтус)			Пол		Примечание
		Вид отделки	Код цвета	S, м²	Вид отделки	Код цвета	S, м²	Вид отделки	Код цвета	L, м	Вид отделки	S, м²	
1	Кухня-гостиная 21,04 м²	ГКЛ по каркасу П113, отм. +2,600; +2,550; окраска, Tikkurila, глубокоматовая	NCS S 0300-N	21,04	Окраска, Tikkurila, полуматовая, подготовка Q3	NCS S 1002-Y50R	41,25	Плинтус МДФ h=110 мм, SX184	NCS S 0300-N	17,7	Аналог: инженерная доска, дуб натуральный, масло, 1-полосная, 14/4 мм, на клею; тип 1, отм. ЧП ±0,000	21,04	Н стен 2600 (до потолка)
2	Спальня 13,95 м²	ГКЛ по каркасу П113, отм. +2,600; +2,550; окраска, Tikkurila, глубокоматовая	NCS S 0300-N	13,95	Окраска, Tikkurila, глубокоматовая, подготовка Q3	NCS S 1502-Y50R	33,91	Плинтус МДФ h=110 мм, SX184	NCS S 0300-N	14,2	Аналог: инженерная доска, дуб натуральный, масло, 1-полосная, 14/4 мм, на клею; тип 1, отм. ЧП ±0,000	13,95	Н стен 2550 (до потолка)
3	Ванная 2,95 м²	ГКЛВ по каркасу П113, отм. +2,600; окраска, Tikkurila, глубокоматовая	NCS S 0300-N	2,95	Облицовка плиткой, 610015000370, 600×1200 мм, клей С2	Italon 610015000370	16,94	нет (облицовка от пола)			Керамогранит, SG651622R, 600×600 мм; тип 2, отм. ЧП −0,015	2,95	Н стен 2615 (до потолка); тёплый пол; гидроизоляция обмазочная, 2 слоя, с заведением на стены 200 мм; над ванной — до 2000 и 300 мм за борт (по пирогу пола); тест проливом и акт скрытых работ
4	Санузел 1,80 м²	ГКЛВ по каркасу П113, отм. +2,600; окраска, Tikkurila, глубокоматовая	NCS S 0300-N	1,80	Облицовка плиткой, 610015000370, 600×1200 мм, клей С2	Italon 610015000370	14,12	нет (облицовка от пола)			Керамогранит, SG651622R, 600×600 мм; тип 2, отм. ЧП −0,015	1,80	Н стен 2615 (до потолка); гидроизоляция обмазочная, 2 слоя, с заведением на стены 200 мм (по пирогу пола); тест проливом и акт скрытых работ
5	Прихожая 9,55 м²	ГКЛ по каркасу П113, отм. +2,550; +2,600; окраска, Tikkurila, глубокоматовая	NCS S 0300-N	9,55	Окраска, Tikkurila, полуматовая, подготовка Q3	NCS S 1502-Y50R	22,66	Плинтус МДФ h=110 мм, SX184	NCS S 0300-N	8,0	Керамогранит, SG651622R, 600×600 мм; тип 3, отм. ЧП ±0,000	9,55	Н стен 2550 (до потолка)
6	Гардеробная 5,94 м²	Существующий потолок, отм. +2,700; окраска, Tikkurila Anti-Reflex 2, глубокоматовая, 2 слоя, подготовка Q3	Tikkurila V503	5,94	Окраска, Tikkurila Harmony, матовая, 2 слоя, подготовка Q3	Tikkurila V503	24,67	Плинтус МДФ h=110 мм, SX184	Tikkurila V503	9,0	Аналог: инженерная доска, дуб натуральный, масло, 1-полосная, 14/4 мм, на клею; тип 1, отм. ЧП ±0,000	5,94	Н стен 2700 (до потолка); плинтус в цвет: стены
	Итого			**55,23**			**153,54**			**48,8**		**55,23**	

Сводка площадей по материалам отделки

Поверхность	Материал / код цвета	Серия	Площадь, м²
Потолок	NCS S 0300-N		49,29
Потолок	Tikkurila V503	Anti-Reflex 2	5,94
Стены	NCS S 1002-Y50R		41,25
Стены	NCS S 1502-Y50R		56,57
Стены	облицовка плиткой 600×1200 мм, Italon 610015000370	610015000370	31,05
Стены	Tikkurila V503	Harmony	24,67

Допущения и предложения на листе

Основа листа: размеры сняты с плана заказчика, контрольный обмер не выполнен (К-5); высота потолка 2700 мм принята: на плане заказчика не указана (К-5); подрайон климата не задан — принят не северный (жилые от 2,5 м) (К-4); толщины стен приняты: наружные 250 мм, перегородки 120 мм — не обмерены (К-5); разрешённая мощность 15 кВт принята по типовой квартире, технических условий нет (К-6).

Знак «**» — предложение проектировщика, заказчиком не утверждено (согласовать с заказчиком): пол пом. 1, 2, 6 — артикул изделия не выбран: позиция описана характеристиками («аналог по характеристикам»), артикул выбирается при закупке.

См. лист открытых вопросов (лист 6, записи К-4–К-6).

Примечания

1. Площади поверхностей — по чистым граням стен до отделки: стены = периметр × высоту от чистого пола помещения до низа потолка минус проёмы (облицовка плиткой — до верха облицовки); плинтус = периметр минус дверные проёмы; пол и потолок — по площади помещения. Количество плиток по раскладке. Площади помещений — с учётом всех частей помещения; откосы в площадь стен не входят.
2. Акцентные стены — отдельными строками, их площадь вычтена из основной отделки стен помещения.
3. Плинтус — длина по периметру за вычетом дверных проёмов; примыкания к наличникам и встроенной мебели — по развёрткам.
4. Формат плитки — Ш×В×Т (ширина × высота в положении укладки × толщина), мм; на полу — вдоль стен А/В × вдоль стен Б/Г.
5. Коды цвета — по веерам производителей; колеровка каждой краски одной партией, проверка выкраса при свете D65 и при лампах проекта.
6. Уровни подготовки Q1–Q4 — система Knauf, не норма ГОСТ/СП; допуски поверхностей — по СП 71.13330.2017 (действующая редакция).
7. «аналог:» — изделие задано характеристиками, марку и артикул согласовать с заказчиком до закупки.

Изм.	Кол.уч	Лист	№ док.	Подп.	Дата
Разраб.		Кырлан А.С.			04.11.26
Пров.					
ГИП					
Н. контр.					
Утв.					

ГД-2026-006-АИ

Квартира 58 м²

Общая площадь 55,23* м² · * размеры приняты, не замерены (реестр — л. 6, 7, К-5)

Дизайн-проект интерьера

Стадия	Лист	Листов
РП	48	87

Ведомость отделки помещений

М б/м

Кырлан Александр Сергеевич

Колерная карта

Цвета и материалы по помещениям · палитра проекта · выкрасы на согласование

Колерная карта по помещениям

Помещение	Поверхность	Образец	Поз.	Система и код цвета	Производитель, линейка / материал, артикул	Блеск	Класс истирания	LRV	Площадь
1. Кухня-гостиная 21,04 м²	стены		**К1**	NCS S 1002-Y50R	Tikkurila	полуматов.	1	82	41,2 м²
	потолок		**К2**	NCS S 0300-N	Tikkurila	глубокомат.	1	92	21,0 м²
	пол		**КМ1**	по образцу	инженерная доска · аналог по хар.				21,0 м²
	плинтус		**К3**	NCS S 0300-N	Orac Decor · Luxxus	полуматов.		92	17,7 м
2. Спальня 13,95 м²	стены		**К4**	NCS S 1502-Y50R	Tikkurila	глубокомат.	2	72	33,9 м²
	потолок		**К5**	NCS S 0300-N	Tikkurila	глубокомат.	2	92	13,9 м²
	пол		**КМ1**	по образцу	инженерная доска · аналог по хар.				13,9 м²
	плинтус		**К3**	NCS S 0300-N	Orac Decor · Luxxus	полуматов.		92	14,2 м
3. Ванная 2,95 м²	стены		**КМ2**	Charme Extra	Italon · арт. 610015000370				16,9 м²
	потолок		**К2**	NCS S 0300-N	Tikkurila	глубокомат.	1	92	3,0 м²
	пол		**КМ3**	Две Венеции / Риальто	Kerama Marazzi · арт. SG651622R				3,0 м²
4. Санузел 1,8 м²	стены		**КМ2**	Charme Extra	Italon · арт. 610015000370				14,1 м²
	потолок		**К2**	NCS S 0300-N	Tikkurila	глубокомат.	1	92	1,8 м²
	пол		**КМ3**	Две Венеции / Риальто	Kerama Marazzi · арт. SG651622R				1,8 м²
5. Прихожая 9,55 м²	стены		**К6**	NCS S 1502-Y50R	Tikkurila	полуматов.	1	72	22,7 м²
	потолок		**К2**	NCS S 0300-N	Tikkurila	глубокомат.	1	92	9,6 м²
	пол		**КМ3**	Две Венеции / Риальто	Kerama Marazzi · арт. SG651622R				9,6 м²
	плинтус		**К3**	NCS S 0300-N	Orac Decor · Luxxus	полуматов.		92	8,0 м
6. Гардеробная 5,94 м²	стены		**К7**	Tikkurila V503	Tikkurila · Harmony	матовая	1	86	24,7 м²
	потолок		**К8**	Tikkurila V503	Tikkurila · Anti-Reflex 2	глубокомат.	2	86	5,9 м²
	пол		**КМ1**	по образцу	инженерная доска · аналог по хар.				5,9 м²
	плинтус		**К9**	Tikkurila V503	Orac Decor · Luxxus			86	9,0 м

Перечень выкрасов на согласование

№	Код	Бренд / веер	Пом. / стена	Подложка	Формат	Статус
1	S 1002-Y50R	NCS Tikkurila	1	ГКЛ с грунтом	600×1000	к выполнению
2	S 0300-N	NCS Tikkurila	1, 2, 3, 4, 5	ГКЛ с грунтом; МДФ под эмаль	600×1000; 300×600	к выполнению
3	S 1502-Y50R	NCS Tikkurila	2, 5	ГКЛ с грунтом	600×1000	к выполнению
4	V503	Tikkurila	6	ГКЛ с грунтом; МДФ под эмаль	600×1000; 300×600	к выполнению

Схема квартиры: цвет стен и акценты (б/м)

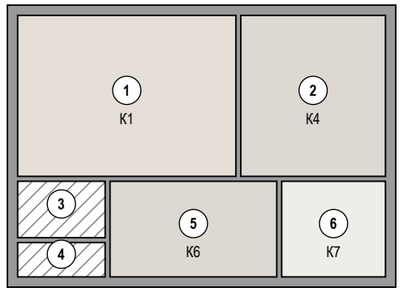


Схема палитры проекта

Стиль: Скандинавский · схема: нейтральная

основной	основной	основной	второстепенный	акцентный
NCS S 1502-Y50R	**NCS S 1002-Y50R**	**NCS S 0300-N**	**Tikkurila V503**	**NCS S 4010-R90B**
тёплый светло-серый LRV 72 стены 2,5	тёплый светлый грейж LRV 82 стены 1	белый LRV 92 потолок 1,2,3,4,5; плинтус 1,2,5	Winter LRV 86 стены 6; потолок 6; плинтус 6	пыльный синий LRV 27 в отделке не применён

План 60/30/10

60%	30%	10%

Окраска, факт — по площади стен, акцентов, потолков

83%	17%

окрашено всего 177,7 м²; второстепенный тон несут мебель и текстиль

Условные обозначения

- **К1** NCS S 1002-Y50R · Tikkurila · полуматов. · кл. 1
- **К2** NCS S 0300-N · Tikkurila · глубокомат. · кл. 1
- **К3** NCS S 0300-N · Orac Decor Luxxus · полуматов.
- **К4** NCS S 1502-Y50R · Tikkurila · глубокомат. · кл. 2
- **К5** NCS S 0300-N · Tikkurila · глубокомат. · кл. 2
- **К6** NCS S 1502-Y50R · Tikkurila · полуматов. · кл. 1
- **К7** Tikkurila V503 · Winter · Harmony · матовая · кл. 1
- **К8** Tikkurila V503 · Winter · Anti-Reflex 2 · глубокомат. · кл. 2
- **К9** Tikkurila V503 · Winter · Luxxus
- **КМ1** аналог: инженерная доска, дуб натуральный, масло, 1-полосная, 14/4 мм
- **КМ2** плитка · 610015000370
- **КМ3** керамогранит · SG651622R

дерево (доска, паркет, ламинат) — рисунок досок

керамогранит, плитка, камень — сетка швов по формату

плашка не залита — цвет только по коду и вееру бренда

К — краска, КМ — отделочный материал (тон КМ — по описанию, эталон — образец материала); кл. — класс истирания (1 — самый стойкий к мытью); LRV — светлота цвета: 0 — чёрный, 100 — белый

Примечания

1. Цвет на листе и на экране — ориентир. До покраски — выкрас на объекте: не меньше А3 (или лист ГКЛ), на грунте под эту краску, не на белой шпаклёвке, в 2 слоя; на обороте — код, бренд, веер, дата. Смотреть днём и вечером, рядом с образцами пола и плитки; к основному цвету стен — ещё 2 соседних оттенка. Красить только в цвет утверждённого выкраса.
2. Краску заказывать по коду из графы «Система и код цвета» у бренда этого кода, не «аналогом» другого; весь объём одного кода — одной партией, колеруемую краску — за один проход машины.
3. Площади — те же, что в ведомости отделки (лист 48); сколько краски заказать — в спецификации отделочных материалов (лист 50).

Допущения и предложения на листе

Основа листа: размеры сняты с плана заказчика, контрольный обмер не выполнен (К-5); высота потолка 2700 мм принята: на плане заказчика не указана (К-5); подрайон климата не задан — принят не северный (жилые от 2,5 м) (К-4); толщины стен приняты: наружные 250 мм, перегородки 120 мм — не обмерены (К-5); разрешённая мощность 15 кВт принята по типовой квартире, технических условий нет (К-6).

Знак «**» — предложение проектировщика, заказчиком не утверждено (согласовать с заказчиком): пол пом. 1, 2, 6 — артикул изделия не выбран: позиция описана характеристиками («аналог по характеристикам»), артикул выбирается при закупке.

См. лист открытых вопросов (лист 6, записи К-4–К-6).

Изм.	Кол.уч	Лист	№ док.	Подп.	Дата
Разраб.		Кырлан А.С.			04.11.26
Пров.					
ГИП					
Н. контр.					
Утв.					

ГД-2026-006-АИ

Квартира 58 м²

Общая площадь 55,23* м² · * размеры приняты, не замерены (реестр — л. 6, 7, К-5)

Дизайн-проект интерьера

Стадия	Лист	Листов
РП	49	87

Колерная карта

М б/м

Кырлан Александр Сергеевич

Спецификация отделочных материалов

Форма 1 по ГОСТ 21.110-2013 · количества — из геометрии проекта, с запасом

ПРЕДВАРИТЕЛЬНО · не для производства работ · открыто пунктов: 10 (реестр — л. 6, 7)

Поз.	Наименование и техническая характеристика	Тип, марка, обозначение документа	Код продукции	Поставщик	Ед. изм.	Кол.	Масса 1 ед., кг	Примечание
	Лакокрасочные материалы							
1	Краска интерьерная водно-дисперсионная акриловая для стен, полуматовая, класс мокрого истирания 1 по EN 13300, база A; цвет NCS S 1002-Y50R, колеровка машинная	Tikkurila		Tikkurila	л	11,7		поз. К1 колерной карты; пом. 1; S = 41,2 м² × 2 сл. × 0,12 л/м² = 9,9 л, +10 % и 0,5 л на подкраску → ≥ 11,4 л; тара 1 × 9 л + 1 × 2,7 л
2	Краска интерьерная водно-дисперсионная для потолков, глубокоматовая, класс мокрого истирания 1 по EN 13300, база A; цвет NCS S 0300-N, колеровка машинная	Tikkurila		Tikkurila	л	9,9		поз. К2 колерной карты; пом. 1, 3, 4, 5; S = 35,3 м² × 2 сл. × 0,12 л/м² = 8,5 л, +10 % и 0,5 л на подкраску → ≥ 9,8 л; тара 1 × 9 л + 1 × 0,9 л
3	Краска интерьерная водно-дисперсионная акриловая для стен, глубокоматовая, класс мокрого истирания 2 по EN 13300, база A; цвет NCS S 1502-Y50R, колеровка машинная	Tikkurila		Tikkurila	л	9,9		поз. К4 колерной карты; пом. 2; S = 33,9 м² × 2 сл. × 0,12 л/м² = 8,1 л, +10 % и 0,5 л на подкраску → ≥ 9,5 л; тара 1 × 9 л + 1 × 0,9 л
4	Краска интерьерная водно-дисперсионная для потолков, глубокоматовая, класс мокрого истирания 2 по EN 13300, база A; цвет NCS S 0300-N, колеровка машинная	Tikkurila		Tikkurila	л	4,5		поз. К5 колерной карты; пом. 2; S = 13,9 м² × 2 сл. × 0,12 л/м² = 3,3 л, +10 % и 0,5 л на подкраску → ≥ 4,2 л; тара 1 × 2,7 л + 2 × 0,9 л
5	Краска интерьерная водно-дисперсионная акриловая для стен, полуматовая, класс мокрого истирания 1 по EN 13300, база A; цвет NCS S 1502-Y50R, колеровка машинная	Tikkurila		Tikkurila	л	7,2		поз. К6 колерной карты; пом. 5; S = 22,7 м² × 2 сл. × 0,12 л/м² = 5,4 л, +10 % и 0,5 л на подкраску → ≥ 6,5 л; тара 2 × 2,7 л + 2 × 0,9 л
6	Краска интерьерная водно-дисперсионная акриловая для стен, матовая, класс мокрого истирания 1 по EN 13300, база A; цвет по вееру Tikkurila V503 «Winter», колеровка машинная	Tikkurila Harmony		Tikkurila	л	7,2		поз. К7 колерной карты; пом. 6; S = 24,7 м² × 2 сл. × 0,12 л/м² = 5,9 л, +10 % и 0,5 л на подкраску → ≥ 7,0 л; тара 2 × 2,7 л + 2 × 0,9 л
7	Краска интерьерная водно-дисперсионная акриловая для потолков, глубокоматовая, класс мокрого истирания 2 по EN 13300, база A; цвет по вееру Tikkurila V503 «Winter», колеровка машинная	Tikkurila Anti-Reflex 2		Tikkurila	л	2,7		поз. К8 колерной карты; пом. 6; S = 5,9 м² × 2 сл. × 0,12 л/м² = 1,4 л, +10 % и 0,5 л на подкраску → ≥ 2,1 л; тара 1 × 2,7 л
8	Акрил, полуматовая в цвет NCS S 0300-N — окраска плинтуса	аналог по характеристикам			л	1,4		поз. К3; пом. 1, 2, 5; L = 39,9 м, S = 5,0 м² × 2 сл. × 0,12 л/м² + 10 %; продукт подобрать в веере NCS
9	Краска для МДФ и дерева в цвет Tikkurila V503 «Winter» — окраска плинтуса; блеск не ниже блеска стен	марка не задана			л	0,5		поз. К9; пом. 6; L = 9,0 м, S = 1,1 м² × 2 сл. × 0,12 л/м² + 10 %; продукт подобрать в веере Tikkurila
10	Грунтовка акриловая под окраску стен и потолков — из системы производителя краски	по системе краски			м²	178		площадь окраски стен, акцентов и потолков; 1 слой перед окраской; расход — по ТУ грунтовки
	Плитка и керамогранит							
11	SG651622R, 600×600 мм, противоскольжение R10	SG651622R		Kerama Marazzi	м²	19,44		шов 2 мм; Ванная, пол; Санузел, пол; Прихожая, пол; по раскладке 48 шт (S = 14,30 м²), с запасом 54 шт
12	610015000370, 1200×600 мм	610015000370		Italon	м²	70,56		шов 2 мм; Ванная, стены А–Г; Ванная, короб стояков Ш1 489×319; Санузел, стены А–Г; Санузел, короб инсталляции; по раскладке 87 шт (S = 31,81 м²), с запасом 98 шт
	Напольные покрытия							
13	Инженерная доска, дуб натуральный, масло, 1-полосная, 14/4 мм, класс 33, эмиссия E1, укладка на клей	аналог по характеристикам			м²	37,5		пом. 1, 2; S = 34,99 м² + 7 % (прямая укладка); к заказу — кратно упаковке
14	Инженерная доска, дуб натуральный, масло, 1-полосная, 14/4 мм, эмиссия E1, укладка на клей	аналог по характеристикам			м²	6,4		пом. 6; S = 5,94 м² + 7 % (прямая укладка); к заказу — кратно упаковке
15	Клей для паркета и инженерной доски, эластичный (СМП / полиуретановый)	по рекомендации производителя доски			м²	41		площадь приклейки; расход и шпатель — по ТУ клея
	Погонажные изделия							
16	SX184, h = 110 мм, крепление к стене, окраска в цвет NCS S 0300-N	SX184		Orac Decor	м	44		пом. 1, 2, 5; L = 39,9 м (периметр без дверных проёмов) + 10 % на подрезку; в штуках — по длине планки
17	SX184, h = 110 мм, крепление к стене, окраска в цвет Tikkurila V503	SX184		Orac Decor	м	10		пом. 6; L = 9,0 м (периметр без дверных проёмов) + 10 % на подрезку; в штуках — по длине планки
	Смеси и материалы для облицовки							
18	Затирка для швов плитки	аналог по характеристикам			кг	3,9		по раскладке (a+b)/(a·b) × шов × t × 1,6 + 10 %
19	Клей плиточный C2 S1 по EN 12004, слой 5 мм	аналог по характеристикам			кг	35		2 меш. по 25 кг; 1,5 кг/м² на 1 мм слоя + 10 %
20	Клей плиточный C2 по EN 12004, слой 5 мм	аналог по характеристикам			кг	332		14 меш. по 25 кг; 1,5 кг/м² на 1 мм слоя + 10 %
21	Гидроизоляция обмазочная мокрых зон: пол, стены по периметру, зоны замачивания; 2 слоя с армирующей лентой в углах	аналог по характеристикам			м²	13,4		площадь по листу раскладки плитки + 10 %; расход смеси — по ТУ
22	Лента демпферная по периметру пола из плитки	аналог по характеристикам			м	21		периметр без дверных проёмов + 10 %

Примечания

1. Количества — из геометрии проекта: площади поверхностей по чистым граням стен до отделки (те же, что в ведомости отделки и колерной карте), плитка, клей и затирка — по раскладке плиточника; в графе «Кол.» — к заказу, с запасом.
2. Краска: расход 0,12 л/м² на слой в 2 слоя, если по ТУ не задан иной; запас 10 % и 0,5 л на подкраску каждого кода. Один код — одна партия, колеровка машинная в колеровочном центре бренда; в заказ — только после утверждения выкраса (колерная карта). Фасовка — по каталогу бренда на дату выпуска; к заказу — не меньше расчётного объёма.
3. «Аналог по характеристикам» — допускается изделие другого производителя с характеристиками не ниже указанных, по согласованию с автором проекта.
4. Графы «Код продукции» и «Масса 1 ед.» не заполнены: коды по классификатору продукции не присвоены, масса единицы до 25 кг (ГОСТ 21.110-2013).
5. Грунтовка и клей для доски указаны площадью обработки; объём — по ТУ выбранного продукта.

Допущения и предложения на листе

Основа листа: размеры сняты с плана заказчика, контрольный обмер не выполнен (К-5); высота потолка 2700 мм принята: на плане заказчика не указана (К-5); подрайон климата не задан — принят не северный (жилые от 2,5 м) (К-4); толщины стен приняты: наружные 250 мм, перегородки 120 мм — не обмерены (К-5); разрешённая мощность 15 кВт принята по типовой квартире, технических условий нет (К-6).

Знак «**» — предложение проектировщика, заказчиком не утверждено (согласовать с заказчиком): пол пом. 1, 2, 6 — артикул изделия не выбран: позиция описана характеристиками («аналог по характеристикам»), артикул выбирается при закупке.

См. лист открытых вопросов (лист 6, записи К-4–К-6).

Изм.	Кол.уч	Лист	№ док.	Подп.	Дата
Разраб.		Кырлан А.С.			04.11.26
Пров.					
ГИП					
Н. контр.					
Утв.					

ГД-2026-006-АИ

Квартира 58 м²

Общая площадь 55,23* м² · * размеры приняты, не замерены (реестр — л. 6, 7, К-5)

Дизайн-проект интерьера

Стадия	Лист	Листов
РП	50	87

Спецификация отделочных материалов

М б/м

Кырлан Александр Сергеевич


Концепция декора и визуализации

Скандинавский · кухня-гостиная и спальня · визуализации, палитра, материалы, ключевые предметы



Вид сверху (3D) — визуализация в работе

Расстановка — по плану мебели (лист 18); шторы, ковры, картины и растения — по плану текстиля и декора.

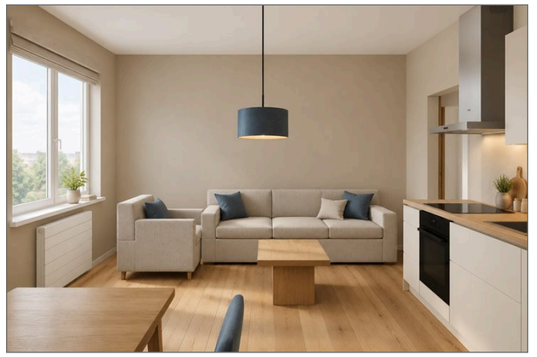

Визуализация 7. Кухня-гостиная (пом. 1)



Визуализация 3. Спальня (пом. 2)



Визуализация 1. Ванная (пом. 3)



Визуализация 11. Санузел (пом. 4)

Палитра 60/30/10 и цвета текстиля



- NCS S 1502-Y50R (тёплый светло-серый), LRV 72 — 60 % база
- NCS S 1002-Y50R (тёплый светлый грейж), LRV 82 — 60 % база
- Tikkurila V503 (Winter), LRV 86 — 30 % второй цвет
- NCS S 4010-R90B (пыльный синий), LRV 27 — 10 % акцент

Материалы и фактуры



Дуб натуральный

пол: пом. 1, 2, 6

Допущения и предложения на листе

Основа листа: размеры сняты с плана заказчика, контрольный обмер не выполнен (К-5); высота потолка 2700 мм принята: на плане заказчика не указана (К-5); подрайон климата не задан — принят не северный (жилые от 2,5 м) (К-4); толщины стен приняты: наружные 250 мм, перегородки 120 мм — не обмерены (К-5); разрешённая мощность 15 кВт принята по типовой квартире, технических условий нет (К-6).

Знак «**» — предложение проектировщика, заказчиком не утверждено (согласовать с заказчиком): ИЗ-2: М1 — Было offset 1300…3500: торец дивана в 500 мм от стены В, правые 350 мм проёма Д-2 (3900…4800) упирались в диван.

См. лист открытых вопросов (лист 6, записи К-4–К-6; лист 7, запись ИЗ-2).

Ключевые предметы

— Диван М1** 2200×950 — кухня-гостиная

— Кровати С1

Настроение

Палитра выведена из выкрасов (колерная карта): база — тёплые нейтрали NCS S 1502-Y50R / S 1002-Y50R на стенах, NCS S 0300-N на потолках; второй цвет — Tikkurila V503 (гардеробная); акцент — пыльный синий NCS S 4010-R90B в текстиле по концепции стиля (текстиль в данных ещё не задан). Настроение стиля: светло, спокойно, уютно (hygge), естественно, функционально, в меру (lagom). Свет тёплый, 2700–3000 K.

Примечания


1. Визуализации — образ интерьера. Изделия, размеры, высоты подвеса и привязки — по чертежам; при расхождении действуют чертежи и ведомости.
2. Коды цвета — ориентир подбора по веерам производителей; ткань утверждается по образцу при дневном свете и при свете проекта 2700–3000 K.
3. Мелкий стайлинг на визуализациях (книги, посуда, свечи) в ведомости не входит и поставляется заказчиком по желанию.

						ГД-2026-006-АИ			
						Квартира 58 м²			
						Общая площадь 55,23* м² · * размеры приняты, не замерены (реестр — л. 6, 7, К-5)			
Изм.	Кол.уч	Лист	№ док.	Подп.	Дата	Дизайн-проект интерьера	Стадия	Лист	Листов
Разраб.		Кырлан А.С.			04.11.26		РП	51	87
Пров.									
ГИП									
						Концепция декора и визуализации	**Кырлан Александр Сергеевич**		
Н. контр.						М б/м			
Утв.									

Встроенная мебель. Схема расположения

встроенная и корпусная мебель на заказ, кухонный гарнитур · размеры в мм · марки — по ведомости изделий

ПРЕДВАРИТЕЛЬНО · не для производства работ · открыто пунктов: 10 (реестр — л. 6, 7)

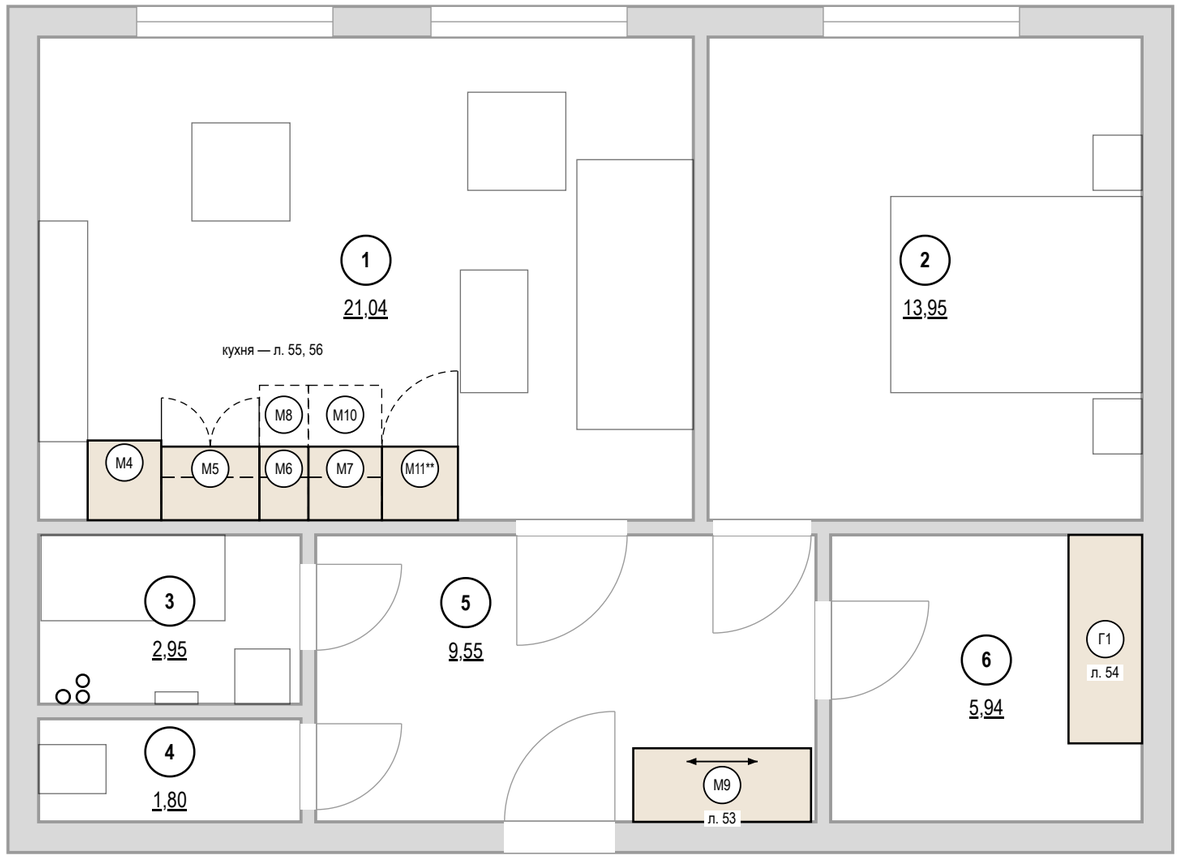

Ведомость изделий

Марка	Наименование	Пом.	Ш×Г×В, мм	Лист
M9	Шкаф-купе	5	1450×600×2450	53
Г1	Система хранения	6	1700×600×2400	54
M11**	Ниша под стиральную машину 620: без корпуса, между боковинами соседних модулей, фасад на петлях к боковине соседнего модуля; цоколь съёмный	1	620×600×900	55
M7	Модуль нижний: ящики, варочная	1	600×600×900	55
M10	Модуль навесной: полки	1	600×350×620	55
M6	Модуль нижний: ящики	1	400×600×900	55
M8	Модуль навесной: полки, сушка	1	1200×350×720	55
M5	Модуль нижний: мойка	1	800×600×900	55
M4	Место под холодильник отдельностоящий: без корпуса и фасада	1	600×650×2100	55

Условные обозначения

- изделие мебельщика: корпус на полу
- невидимый контур: навесной модуль, корпус под столешницей
- открывание распашного фасада
- зона выдвижения ящика, двери техники
- дверь купе, стрелка — направление движения
- K1 — марка изделия или модуля (на схеме расположения под ней — лист изделия)

Допущения и предложения на листе

Основа листа: размеры сняты с плана заказчика, контрольный обмер не выполнен (К-5); высота потолка 2700 мм принята: на плане заказчика не указана (К-5); подрайон климата не задан — принят не северный (жилые от 2,5 м) (К-4); толщины стен приняты: наружные 250 мм, перегородки 120 мм — не обмерены (К-5); разрешённая мощность 15 кВт принята по типовой квартире, технических условий нет (К-6).

Знак «**» — предложение проектировщика, заказчиком не утверждено (согласовать с заказчиком): К-7: M11 — место стиральной машины: вместо модуля с ящиками 400 справа от варочной; ряд до 3420, журнальный стол M21 (с х 3440) не мешает загрузке.

См. лист открытых вопросов (лист 6, записи К-4–К-7).

Примечания

1. Изделия — по чистовым размерам помещений; перед раскроем — контрольный замер цеха после чистовой отделки стен, пола и потолка.
2. Открывание фасадов и выдвижение ящиков показано в открытом положении: зоны не пересекают двери, радиаторы, выключатели и проходы.
3. Стояки и счётчики за мебелью — с сервисным люком; газовые трубы мебелью не зашиваются.
4. Покупная мебель — по плану расстановки мебели и спецификации дизайнера; здесь — подложкой.

1000 мм · печать 1:1

Изм.	Кол.уч	Лист	№ док.	Подп.	Дата
Разраб.		Кырлан А.С.			04.11.26
Пров.					
ГИП					
Н. контр.					
Утв.					

ГД-2026-006-АИ

Квартира 58 м²

Общая площадь 55,23* м² · * размеры приняты, не замерены (реестр — л. 6, 7, К-5)

Дизайн-проект интерьера

Стадия	Лист	Листов
РП	52	87

Встроенная мебель. Схема расположения

М 1:50

Кырлан Александр Сергеевич


выпуск 04.11.2026 № 94e55e632e · стр. 59 из 96

Шкаф-купе М9


Прихожая (пом. 5) · вид из помещения · размеры в мм, отметки в м

ПРЕДВАРИТЕЛЬНО · не для производства работ · открыто пунктов: 10 (реестр — л. 6, 7)


Вид с фасадами

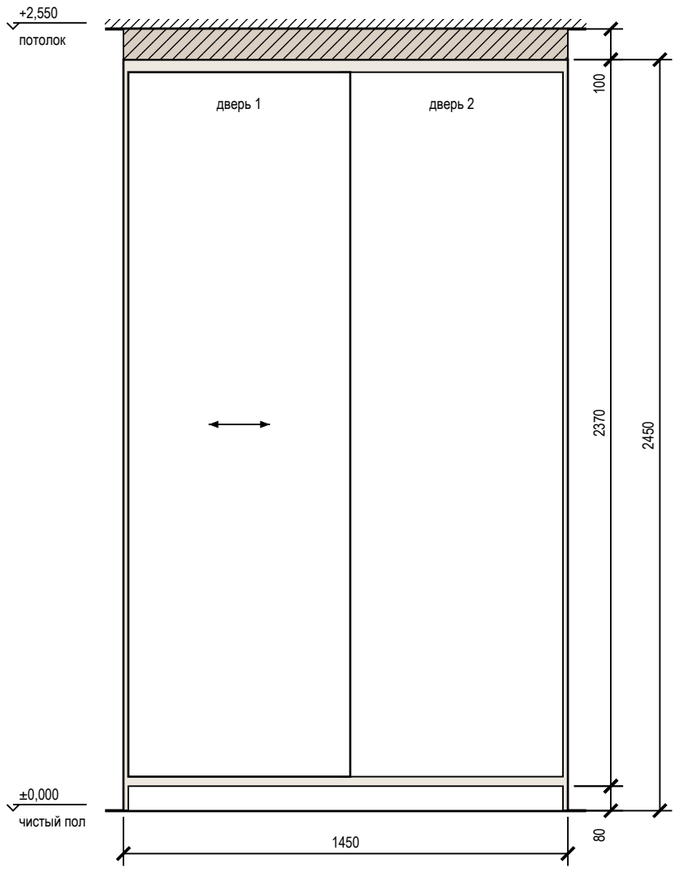


Вид без фасадов

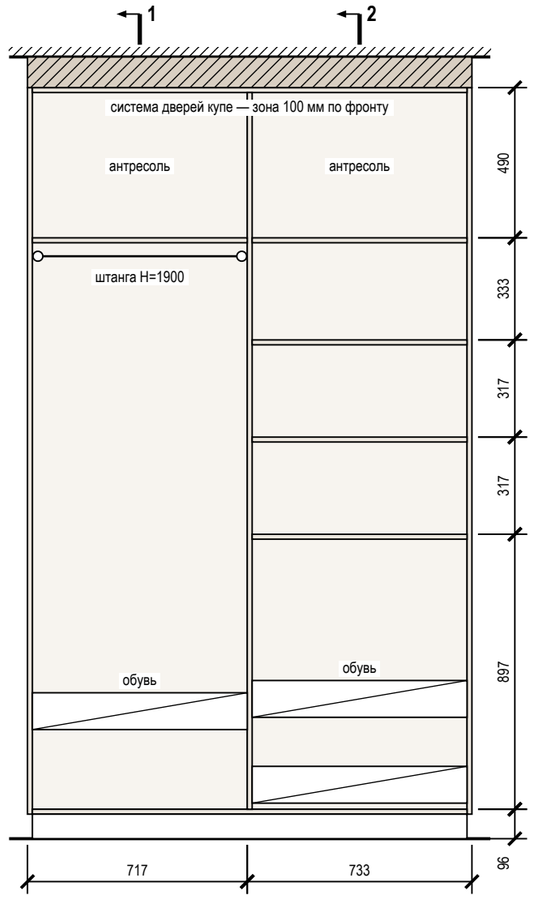

Разрез 1-1

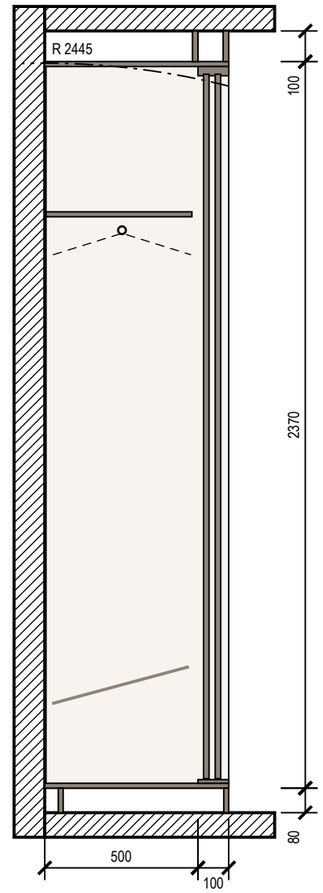

Разрез 2-2

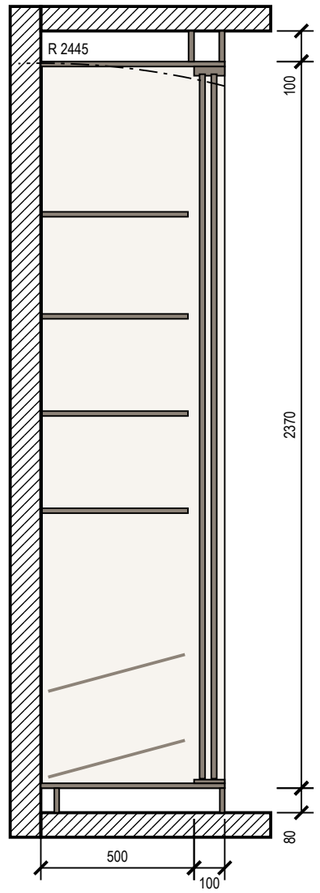

Примечания

1. Размеры — в мм по чистовой отделке; изделие 1450×600×2450 (Ш×Г×В). Перед раскроем — контрольный замер цеха после чистовой отделки стен, пола и потолка.
2. Корпус — ЛДСП 16 мм, задняя стенка ХДФ 4 мм в паз, цоколь 80 мм на регулируемых опорах; двери купе — ЛДСП 10 мм в алюминиевом профиле; нахлёст 30 мм, ширина двери 724 мм, высота — проём минус 40 мм; цвет — по колерной карте.
3. Кромка: скрытые торцы 0,4 мм, видимые 1 мм (ПВХ/АБС).
4. Номинальные зазоры: дверь купе — боковина 3 мм, фасад ящика — стойка 2 мм; ящики внутри купе — с накладкой 30 мм на стойке со стороны нахлёста дверей.
5. Присадка по 32-й системе — выполняет цех.
6. Компенсатор 100 мм — короб из ЛДСП по фронту и торцам, подгоняется к потолку при монтаже (припуск 20 мм), крепится к корпусу и к потолку.
7. Подъём корпуса: диагональ боковины без цоколя $\sqrt{(2370^2 + 600^2)} = 2445$ мм < 2550 мм до потолка — корпус собирается лёжа, поднимается поворотом и ставится на цоколь.
8. Крепление к стене от опрокидывания — уголки 2 шт. к несущему основанию (монтажная схема шкафов).

Условные обозначения

- дверь купе, стрелка — направление движения
- корпус и полки ЛДСП (вид на стену)
- задняя стенка ХДФ
- деталь в разрезе
- компенсатор — короб до потолка
- штанга для плечиков (на разрезе — плечики 450 мм)
- траектория угла корпуса при подъёме в проектное положение

Допущения и предложения на листе

Основа листа: размеры сняты с плана заказчика, контрольный обмер не выполнен (К-5); высота потолка 2700 мм принята: на плане заказчика не указана (К-5); подрайон климата не задан — принят не северный (жилые от 2,5 м) (К-4); толщины стен приняты: наружные 250 мм, перегородки 120 мм — не обмерены (К-5); разрешённая мощность 15 кВт принята по типовой квартире, технических условий нет (К-6).

См. лист открытых вопросов (лист 6, записи К-4–К-6).

1000 мм · печать 1:1

Изм.	Кол.уч	Лист	№ док.	Подп.	Дата
Разраб.		Кырлан А.С.			04.11.26
Пров.					
ГИП					
Н. контр.					
Утв.					

ГД-2026-006-АИ

Квартира 58 м²

Общая площадь 55,23* м² · * размеры приняты, не замерены (реестр — л. 6, 7, К-5)

Дизайн-проект интерьера

Стадия	Лист	Листов
РП	53	87

Шкаф-купе М9

М 1:20

Кырлан Александр Сергеевич


выпуск 04.11.2026 № 94e55e632e · стр. 60 из 96

Система хранения Г1


Гардеробная (пом. 6) · вид из помещения · размеры в мм, отметки в м

ПРЕДВАРИТЕЛЬНО · не для производства работ · открыто пунктов: 10 (реестр — л. 6, 7)


Общий вид

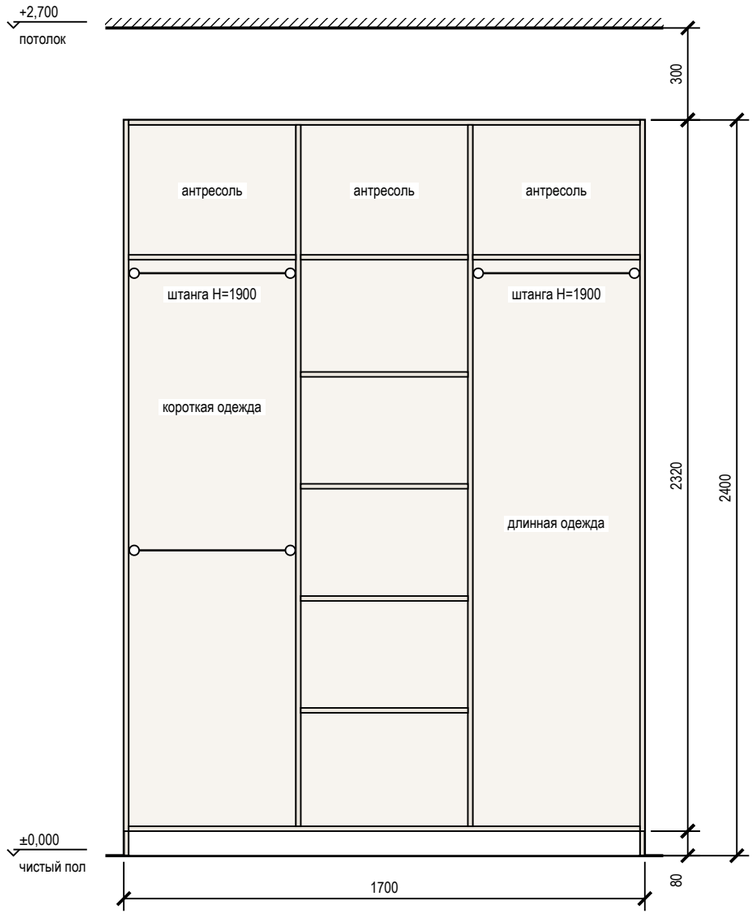


Наполнение, размеры в свету

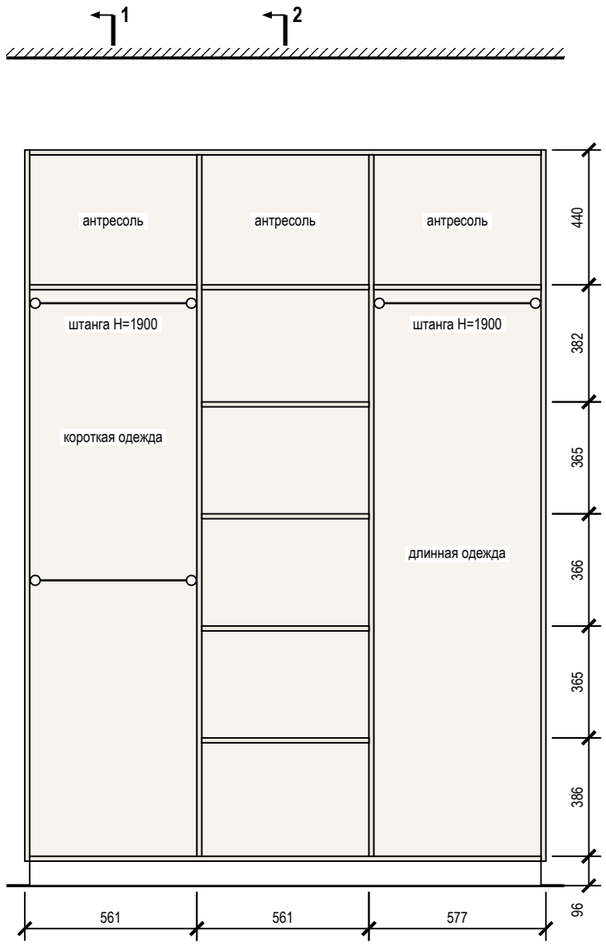

Разрез 1-1

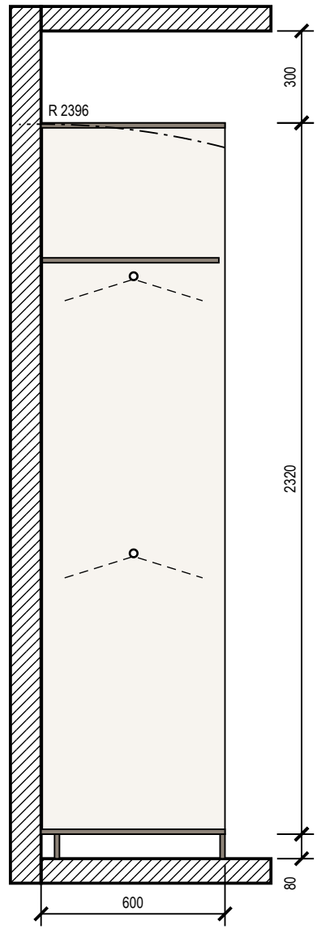

Разрез 2-2

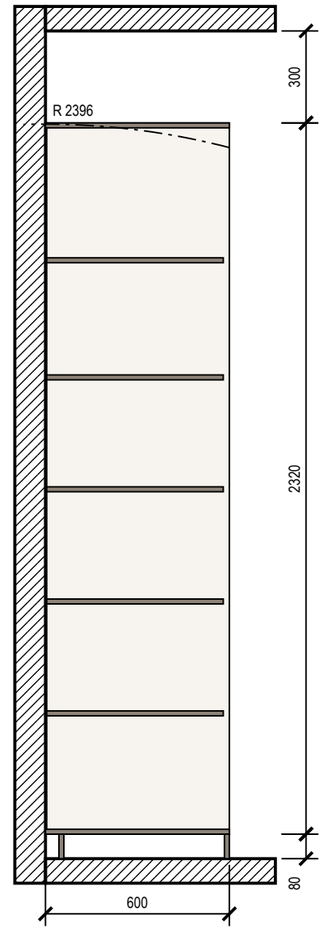

Примечания

1. Размеры — в мм по чистовой отделке; изделие 1700×600×2400 (Ш×Г×В). Перед раскроем — контрольный замер цеха после чистовой отделки стен, пола и потолка.
2. Корпус — ЛДСП 16 мм, задняя стенка ХДФ 4 мм в паз, цоколь 80 мм на регулируемых опорах; открытая система: без фасадов.
3. Кромка: скрытые торцы 0,4 мм, видимые 2 мм (ПВХ/АБС).
4. Присадка по 32-й системе — выполняет цех.
5. Зазор до потолка 300 мм.
6. Подъём корпуса: диагональ боковины без цоколя √(2320² + 600²) = 2396 мм < 2700 мм до потолка — корпус собирается лёжа, поднимается поворотом и ставится на цоколь.
7. Крепление к стене от опрокидывания: крепление к стене, 3 точки; основание стены и шаг анкеров — монтажная схема шкафов.

Условные обозначения

- корпус и полки ЛДСП (вид на стену)
- задняя стенка ХДФ
- деталь в разрезе
- штанга для плечиков (на разрезе — плечики 450 мм)
- траектория угла корпуса при подъёме в проектное положение

Допущения и предложения на листе

Основа листа: размеры сняты с плана заказчика, контрольный обмер не выполнен (К-5); высота потолка 2700 мм принята: на плане заказчика не указана (К-5); подрайон климата не задан — принят не северный (жилые от 2,5 м) (К-4); толщины стен приняты: наружные 250 мм, перегородки 120 мм — не обмерены (К-5); разрешённая мощность 15 кВт принята по типовой квартире, технических условий нет (К-6).

См. лист открытых вопросов (лист 6, записи К-4–К-6).

1000 мм · печать 1:1

Изм.	Кол.уч	Лист	№ док.	Подп.	Дата
Разраб.		Кырлан А.С.			04.11.26
Пров.					
ГИП					
Н. контр.					
Утв.					

ГД-2026-006-АИ

Квартира 58 м²

Общая площадь 55,23* м² · * размеры приняты, не замерены (реестр — л. 6, 7, К-5)

Дизайн-проект интерьера

Стадия	Лист	Листов
РП	54	87

Система хранения Г1

М 1:20

Кырлан Александр Сергеевич


выпуск 04.11.2026 № 94e55e632e · стр. 61 из 96

Кухня (пом. 1). Развёртка гарнитура


Кухня-гостиная (пом. 1) · стена В · вид из помещения · размеры в мм, отметки в м

ПРЕДВАРИТЕЛЬНО · не для производства работ · открыто пунктов: 10 (реестр — л. 6, 7)


Вид с фасадами

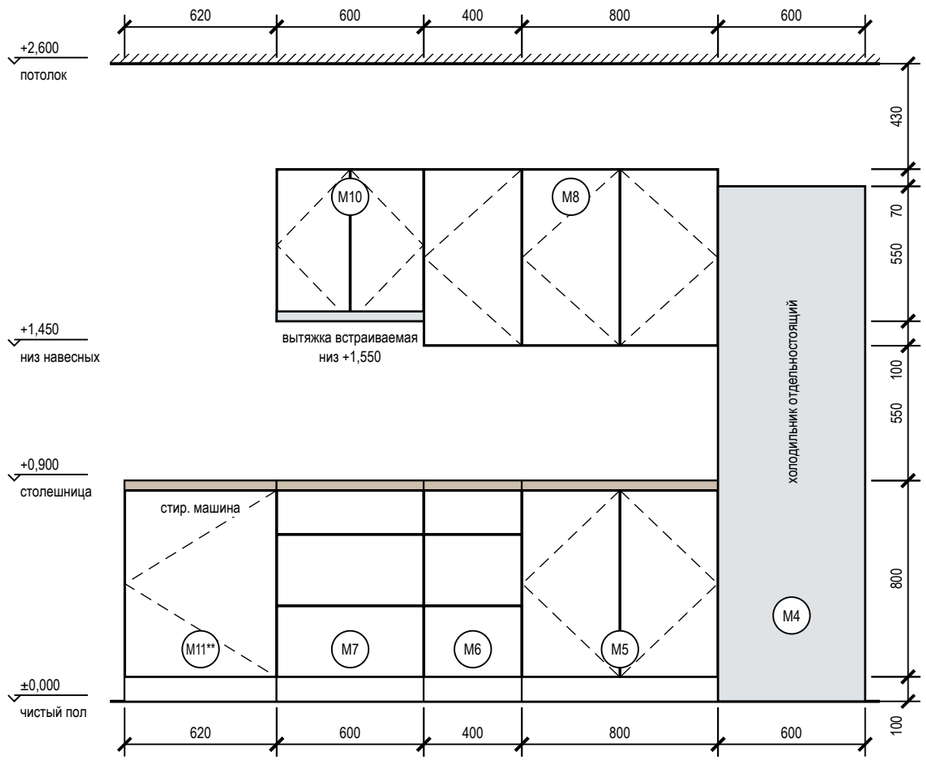


Вид без фасадов (наполнение, выводы)

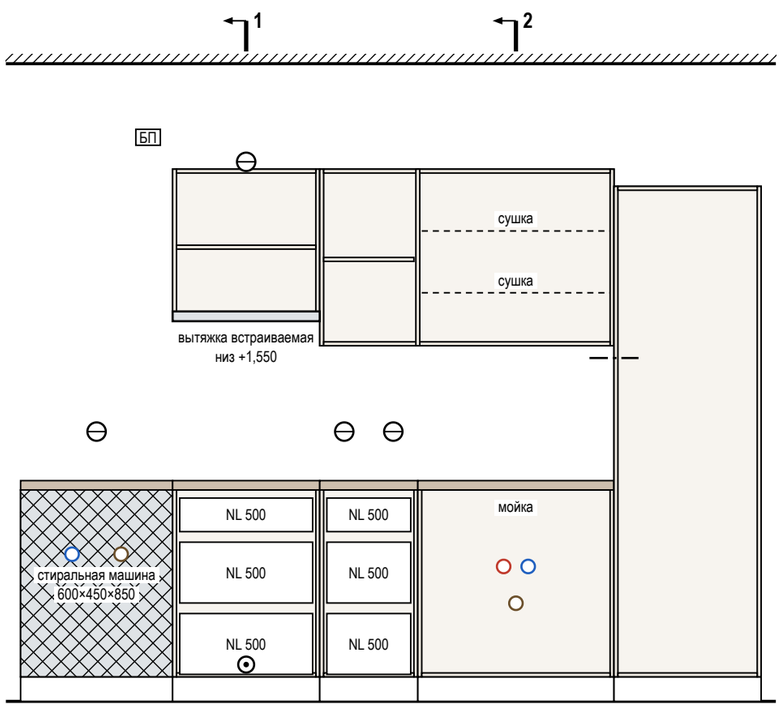

Разрез 1-1

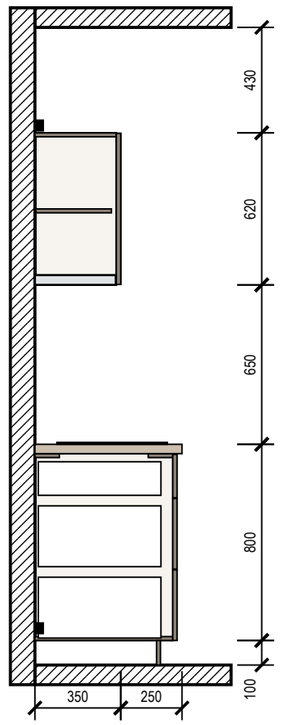

Разрез 2-2

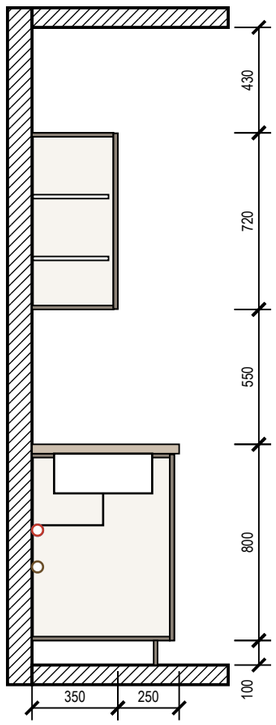

1000 мм · печать 1:1

Условные обозначения

- фасад распашной: линии сходятся к стороне петель
- фасад ящика, карго
- встраиваемая техника
- столешница
- доборная планка
- деталь в разрезе
- К1 — марка изделия или модуля (на схеме расположения под ней — лист изделия)
- розетка на стене
- вывод кабеля к технике
- В1 — вывод воды В1 / Т3, канализации К1

Примечания

1. Размеры — в мм по чистовой отделке, вид из помещения; марки — как на плане расстановки. Перед раскроем — контрольный замер цеха после фартука и пола.
2. Корпуса — ЛДСП 16 мм, задняя стенка ХДФ 4 мм; фасады — МДФ эмаль 18 мм, цвет по колерной карте; столешница 38 мм, свес 20 мм; цоколь 100 мм.
3. Кромка: скрытые торцы 0,4 мм, видимые 1 мм. Номинальные зазоры: между фасадами 3 мм, фасад — столешница 3 мм, фасад — стена не менее 3 мм.
4. Ящики полного выдвижения и петли — с доводчиком; присадка по 32-й системе — выполняет цех.
5. Вытяжка встраивается в дно навесного модуля М10 над варочной: её низ на 1550 мм от пола, 650 мм над панелью (не меньше 650 мм).
6. Ниши техники — по монтажным схемам выбранных моделей: решётка в цоколе и канал за пеналом холодильника, зазор за духовым шкафом, фасад ПММ на двери машины.

Допущения и предложения на листе

Основа листа: размеры сняты с плана заказчика, контрольный обмер не выполнен (К-5); высота потолка 2700 мм принята: на плане заказчика не указана (К-5); подрайон климата не задан — принят не северный (жилые от 2,5 м) (К-4); толщины стен приняты: наружные 250 мм, перегородки 120 мм — не обмерены (К-5); разрешённая мощность 15 кВт принята по типовой квартире, технических условий нет (К-6).

Знак «**» — предложение проектировщика, заказчиком не утверждено (согласовать с заказчиком): К-7: М11 — место стиральной машины: вместо модуля с ящиками 400 справа от варочной; ряд до 3420, журнальный стол М21 (с х 3440) не мешает загрузке.

См. лист открытых вопросов (лист 6, записи К-4–К-7).

Изм.	Кол.уч	Лист	№ док.	Подп.	Дата
Разраб.		Кырлан А.С.			04.11.26
Пров.					
ГИП					
Н. контр.					
Утв.					

ГД-2026-006-АИ

Квартира 58 м²

Общая площадь 55,23* м² · * размеры приняты, не замерены (реестр — л. 6, 7, К-5)

Дизайн-проект интерьера

Стадия	Лист	Листов
РП	55	87

Кухня (пом. 1). Развёртка гарнитура

М 1:25

Кырлан Александр Сергеевич


выпуск 04.11.2026 № 94e55e632e · стр. 62 из 96

Кухня (пом. 1). Монтажная схема


Кухня-гостиная (пом. 1) · стена В · размеры в мм от чистых поверхностей, высоты — от чистого пола

ПРЕДВАРИТЕЛЬНО · не для производства работ · открыто пунктов: 10 (реестр — л. 6, 7)

Привязка выводов и крепление модулей

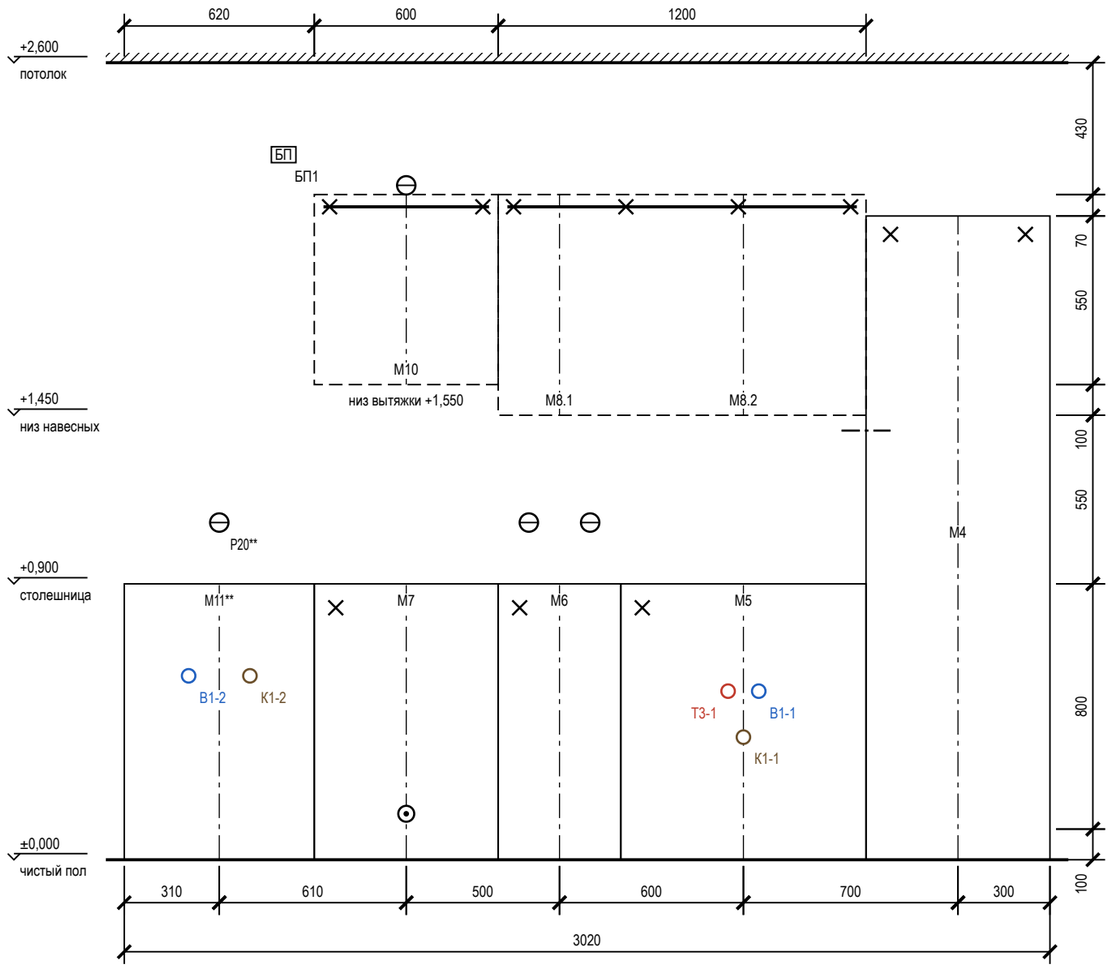

План столешницы

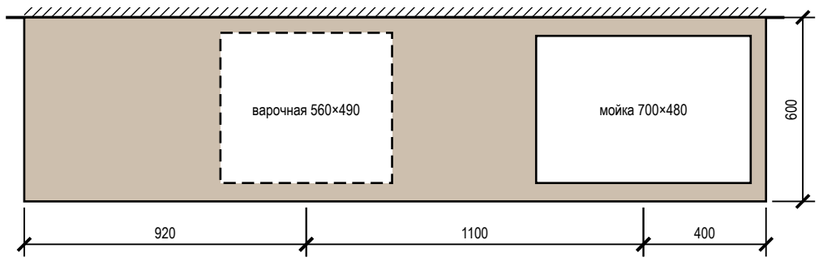

Привязка выводов к осям модулей

Код	Назначение	Модуль	От оси, мм	Н, мм	Размещение
B1-2	B1 — кран машины	M11**	−100	600	в нише стиральной машины, за машиной (доступ — выдвинуть машину)
P20**	розетка — стиральная машина	M11**	0	1100	над столешницей (фартук)
K1-2	K1 Ø40 — стиральная машина	M11**	+100	600	в нише стиральной машины, за машиной (доступ — выдвинуть машину)
БП1	блок питания	M11**	+210	2300	над столешницей (фартук)
	вывод кабеля — варочная панель	M7	0	150	в соседнем модуле, за ящиком
	розетка — вытяжка (встроена в дно M10)	M10	0	2200	в навесном модуле
	розетка — рабочая зона	M6	−100	1100	над столешницей (фартук)
	розетка ×2 — рабочая зона	M6	+100	1100	над столешницей (фартук)
T3-1	T3 — межос. 100	M5	−50	550	в модуле мойки
K1-1	K1 Ø50 — мойка	M5	0	400	в модуле мойки
B1-1	B1 — межос. 100	M5	+50	550	в модуле мойки
	светодиодная лента — подсветка столешницы	M4	−300	1400	за пеналом

Зазоры под отделку

Поверхность	Отделка	Зазор, мм	Учесть
фартук	плитка / стеновая панель	10	от чернового основания до корпуса навесных и столешницы
стены	окраска	5	под штукатурку и шпаклёвку за пеналом
пол	инженерная доска		цоколь — после укладки пола, опоры ±20 мм

Условные обозначения

- нижний модуль, пенал (контур)
- невидимый контур: навесной модуль, корпус под столешницей
- ось модуля (от неё — привязка вывода)
- анкер / уголок крепления к стене
- розетка на стене
- вывод кабеля к технике
- B1 — вывод воды B1 / T3, канализации K1

Допущения и предложения на листе

Основа листа: размеры сняты с плана заказчика, контрольный обмер не выполнен (К-5); высота потолка 2700 мм принята: на плане заказчика не указана (К-5); подрайон климата не задан — принят не северный (жилые от 2,5 м) (К-4); толщины стен приняты: наружные 250 мм, перегородки 120 мм — не обмерены (К-5); разрешённая мощность 15 кВт принята по типовой квартире, технических условий нет (К-6).

Знак «**» — предложение проектировщика, заказчиком не утверждено (согласовать с заказчиком): К-7: M11 — место стиральной машины: вместо модуля с ящиками 400 справа от варочной; ряд до 3420, журнальный стол M21 (с х 3440) не мешает загрузке; P20 — питание стиральной машины П6 — отдельная группа 6 (УЗО 30 мА); над столешницей в габарите машины, не за корпусом.

См. лист открытых вопросов (лист 6, записи К-4–К-7).

Примечания

1. Выводы — по проекту электрики и ВК; привязка по горизонтали — от оси модуля (плюс — вправо по виду), по высоте — от чистого пола до оси вывода.
2. Пенал — уголки к стене 2 шт. сверху; нижние модули — стяжками между собой и уголком к стене; ряд выставить по уровню опорами цоколя.
3. Розетки над столешницей — не ниже 150 мм над ней и не за корпусом техники; розетка за ПММ, духовым шкафом и холодильником — только в соседнем модуле или в зоне цоколя с доступом.
4. Столешница — вырезы по шаблонам выбранных моделей мойки и варочной панели; торцы у стены — герметик, пристеночный плинтус.

1000 мм · печать 1:1

Изм.	Кол.уч	Лист	№ док.	Подп.	Дата
Разраб.		Кырлан А.С.			04.11.26
Пров.					
ГИП					
Н. контр.					
Утв.					

ГД-2026-006-АИ

Квартира 58 м²

Общая площадь 55,23* м² · * размеры приняты, не замерены (реестр — л. 6, 7, К-5)

Дизайн-проект интерьера

Стадия	Лист	Листов
РП	56	87

Кухня (пом. 1). Монтажная схема

М 1:20

Кырлан Александр Сергеевич


выпуск 04.11.2026 № 94e55e632e · стр. 63 из 96

Шкафы. Монтажная схема


крепление к стене, установочные размеры, зазоры под отделку · размеры в мм

ПРЕДВАРИТЕЛЬНО · не для производства работ · открыто пунктов: 10 (реестр — л. 6, 7)

Шкаф-купе М9 (пом. 5)

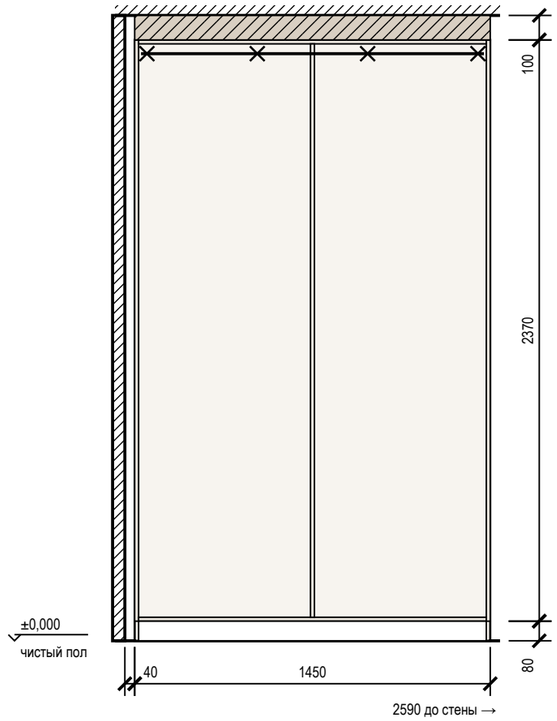

Система хранения Г1 (пом. 6)

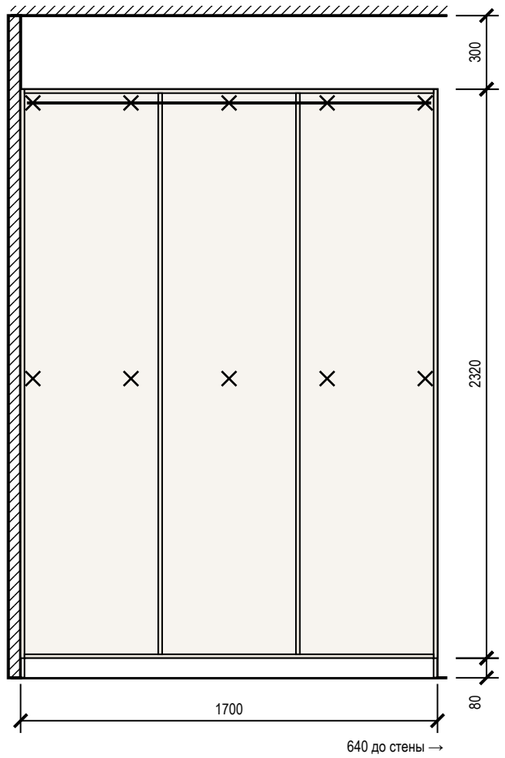

Крепление и зазоры под отделку

Марка	Помещение, стена	Основание	Отделка стены	Зазор, мм	Крепёж по планке	От опрокидывания
М9	Прихожая (5), стена В	по основанию — см. таблицу крепежа	окраска	5	анкер 4 шт., шаг 450	уголки 2 шт.
Г1	Гардеробная (6), стена Б	по основанию — см. таблицу крепежа	окраска	5	анкер 10 шт. (2 ряда)	крепление к стене, 3 точки

Крепёж по основанию стены

Основание стены	Крепёж
бетон, ж/б	анкер-шуруп 7,5×72 или дюбель 8×60 с шурупом 5×70
кирпич полнотелый	дюбель 8×80 с шурупом 5×90
газобетон, пазогребень	дюбель для газобетона 10×100 или химический анкер
гипсокартон	закладная до обшивки (брус 40×80 или фанера 18 мм), саморез в закладную

Условные обозначения

- анкер / уголок крепления к стене
- корпус и полки ЛДСП (вид на стену)
- компенсатор — короб до потолка

Примечания

1. Установочные размеры — от чистого пола и чистых стен; перед установкой контрольный замер после отделки.
2. Порядок: корпус выставить по уровню опорами цоколя → закрепить к стене по задней планке → навесить двери и фасады, отрегулировать зазоры → подогнать и закрепить компенсатор.
3. Анкеры — с шагом не более 500 мм, не ближе 50 мм от края планки; на ГКЛ только в закладную, установленную до обшивки.
4. Скрытые коммуникации под анкеры проверить детектором; трассы электрики по плану розеток.

Допущения и предложения на листе

Основа листа: размеры сняты с плана заказчика, контрольный обмер не выполнен (К-5); высота потолка 2700 мм принята: на плане заказчика не указана (К-5); подрайон климата не задан — принят не северный (жилые от 2,5 м) (К-4); толщины стен приняты: наружные 250 мм, перегородки 120 мм — не обмерены (К-5); разрешённая мощность 15 кВт принята по типовой квартире, технических условий нет (К-6).
См. лист открытых вопросов (лист 6, записи К-4–К-6).

1000 мм · печать 1:1

Изм.	Кол.уч	Лист	№ док.	Подп.	Дата
Разраб.		Кырлан А.С.			04.11.26
Пров.					
ГИП					
Н. контр.					
Утв.					

ГД-2026-006-АИ

Квартира 58 м²

Общая площадь 55,23* м² · * размеры приняты, не замерены (реестр — л. 6, 7, К-5)

Дизайн-проект интерьера

Стадия	Лист	Листов
РП	57	87

Шкафы. Монтажная схема

М 1:25

Кырлан Александр Сергеевич

выпуск 04.11.2026 № 94e55e632e · стр. 64 из 96

Ведомости изделий, техники и фурнитуры

встроенная мебель и кухонный гарнитур · размеры в мм

Ведомость изделий

Марка	Наименование	Пом.	Ш×Г×В, мм	Корпус	Фасад	Кромка, мм	Кол.
М9	Шкаф-купе	5	1450×600×2450	ЛДСП 16	ЛДСП 10 мм в алюминиевом профиле	0,4 / 1	1
Г1	Система хранения	6	1700×600×2400	ЛДСП 16	без фасадов	0,4 / 2	1
М11**	Ниша под стиральную машину 620: без корпуса, между боковинами соседних модулей, фасад на петлях к боковине соседнего модуля; цоколь съёмный	1	620×600×900	без корпуса	МДФ эмаль 18 мм — на дверь машины (навеска из её комплекта), цоколь		1
М7	Модуль нижний: ящики, варочная	1	600×600×900	ЛДСП 16	МДФ эмаль 18 мм	0,4 / 1	1
М10	Модуль навесной: полки	1	600×350×620	ЛДСП 16	МДФ эмаль 18 мм	0,4 / 1	1
М6	Модуль нижний: ящики	1	400×600×900	ЛДСП 16	МДФ эмаль 18 мм	0,4 / 1	1
М8	Модуль навесной: полки, сушка	1	1200×350×720	ЛДСП 16	МДФ эмаль 18 мм	0,4 / 1	1
М5	Модуль нижний: мойка	1	800×600×900	ЛДСП 16	МДФ эмаль 18 мм	0,4 / 1	1
М4	Место под холодильник отдельностоящий: без корпуса и фасада	1	600×650×2100 (место в ряду)	без корпуса	без фасада (прибор отдельностоящий)		

Ведомость встраиваемой техники

Поз.	Прибор	Ниша, вырез, мм	Вентиляция	Питание	Схема
М7	Варочная панель индукционная, 60 см	вырез в столешнице 560 × 490		М7, Н=150 — в соседнем модуле, за ящиком	по модели
М5	Мойка врезная / подстольная с сифоном	вырез по шаблону, ориентир 700 × 480		смеситель — выводы ВК	по модели
М4	Холодильник отдельностоящий	проём 600, зазор сверху ≥ 50	по паспорту модели	питание: точка ЭОМ не задана — вывод под прибор не делать до задания	по модели
М10	Вытяжка встраиваемая в навесной модуль, 60 см	низ ≥ 650 над панелью	воздуховод к вентканалу, короб до потолка	питание: точка ЭОМ не задана — вывод под прибор не делать до задания	по модели

Ведомость фурнитуры

№	Фурнитура	Тип, размер	Изделия	Кол.
1	Система дверей купе: профиль, направляющие, ролики	на 2 двери	М9	1
2	Ручка-профиль вертикальная	в цвет профиля	М9	2
3	Полкодержатель с фиксацией	ø5 мм	М9, Г1, М10, М8	56
4	Штанга овальная 30×15, L = 701	+ 2 держателя	М9	1
5	Полка для обуви выдвижная наклонная	ширина 701	М9	3
6	Опора регулируемая с цоколем на клипсах	ход 20 мм	М9, Г1	14
7	Анкер по основанию стены	по таблице крепежа	М9, Г1, М10, М8	20
8	Уголок крепления к стене от опрокидывания	стальной	М9, Г1	4
9	Штанга овальная 30×15, L = 545	+ 2 держателя	Г1	3
10	Петля накладная 110° с доводчиком	чашка 35 мм	М11**, М10, М8, М5	16
11	Ручка-профиль	латунь матовая	М11**, М7, М10, М6, М8, М5	14
12	Направляющие полного выдвижения с доводчиком NL 500	пара	М7, М6	6
13	Опора кухонная регулируемая 100–120 мм	+ клипса цоколя	М7, М6, М5	14
14	Навес регулируемый для навесного шкафа	пара на секцию	М10, М8	3
15	Шина монтажная	L = 540	М10	1
16	Сушка для посуды в шкаф	ширина 800	М8	1
17	Шина монтажная	L = 1140	М8	1

Примечания

1. Модели техники выбирает заказчик до изготовления мебели; ниши, вырезы и вентиляция — по монтажной схеме выбранной модели (условие гарантии), её номер вносится в ведомость.
2. Количество фурнитуры — по чертежам изделий; запас крепежа 5 %. Аналоги — по характеристикам (доводчик, нагрузка, ход).
3. Цвет корпусов, фасадов и профилей — по колерной карте проекта. Кромка — скрытые / видимые торцы, мм.

Допущения и предложения на листе

Основа листа: размеры сняты с плана заказчика, контрольный обмер не выполнен (К-5); высота потолка 2700 мм принята: на плане заказчика не указана (К-5); подрайон климата не задан — принят не северный (жилые от 2,5 м) (К-4); толщины стен приняты: наружные 250 мм, перегородки 120 мм — не обмерены (К-5); разрешённая мощность 15 кВт принята по типовой квартире, технических условий нет (К-6).

Знак «**» — предложение проектировщика, заказчиком не утверждено (согласовать с заказчиком): К-7: М11 — место стиральной машины: вместо модуля с ящиками 400 справа от варочной; ряд до 3420, журнальный стол М21 (с х 3440) не мешает загрузке.

Изменения по листу без подписи: ИЗ-1.

См. лист открытых вопросов (лист 6, записи К-4–К-7; лист 7, запись ИЗ-1).

Изм.	Кол.уч	Лист	№ док.	Подп.	Дата
Разраб.		Кырлан А.С.			04.11.26
Пров.					
ГИП					
Н. контр.					
Утв.					

ГД-2026-006-АИ

Квартира 58 м²

Общая площадь 55,23* м² · * размеры приняты, не замерены (реестр — л. 6, 7, К-5)

Дизайн-проект интерьера

Стадия	Лист	Листов
РП	58	87

Ведомости изделий, техники и фурнитуры

М б/м

Кырлан Александр Сергеевич

08

Развёртки и узлы



Кырлан Александр Сергеевич

выпуск 04.11.2026 № 94e55e632e · стр. 66 из 96

Реестр марок отделки и позиций альбома

Реестр марок отделки (О ↔ позиции колерной карты) и марки позиций по видам

Реестр марок отделки альбома

Марка	Поверхность	Материал, изделие	Цвет, код	Помещения	Колер. карта
О1	стены	окраска, Tikkurila, шелковисто-матовая, подготовка Q3	NCS S 1002-Y50R	1	К1
О2	плинтус	плинтус МДФ, Orac Decor Luxxus, h 110 мм, SX184, шелковисто-матовая	NCS S 0300-N	1, 2, 5	К3
О3	потолок	окраска, Tikkurila, глубокоматовая	NCS S 0300-N	1, 2, 3, 4, 5	К2, К5
О4	пол	инженерная доска, аналог: инженерная доска, дуб натуральный, масло, 1-полосная, 14/4 мм		1, 2, 6	КМ1
О5	стены	окраска, Tikkurila, глубокоматовая, подготовка Q3	NCS S 1502-Y50R	2, 5	К4, К6
О6	стены	облицовка плиткой, Italon Charme Extra, 600×1200 мм, 610015000370	Italon 610015000370 «Charme Extra»	3, 4	КМ2
О7	пол	керамогранит, Kerama Marazzi Две Венеции / Риальто, 600×600 мм, SG651622R	Kerama Marazzi SG651622R «Две Венеции / Риальто»	3, 4, 5	КМ3
О8	стены	окраска, Tikkurila Harmony, матовая, подготовка Q3	Tikkurila V503 «Winter»	6	К7
О9	плинтус	плинтус МДФ, Orac Decor Luxxus, h 110 мм, SX184	Tikkurila V503 «Winter»	6	К9
О10	потолок	окраска, Tikkurila Anti-Reflex 2, глубокоматовая, подготовка Q3	Tikkurila V503 «Winter»	6	К8

Марки позиций альбома по видам

Префикс	Что обозначает, позиции	Листы
Д	двери: Д-1–Д-4	14–16
ОК	окна: ОК-1	14–16
Г, М, С	мебель и оборудование: Г1, М1**, М3–М10, М11**, М20, М21, М22**, С1–С3	17–19
П	сантехнические приборы: П1**, П3**, П4, П5, П6**, П20	29–38
Р	розетки: Р1–Р16, Р20**	20–26
ЭВ	выводы кабеля: ЭВ1–ЭВ3	20–26
S	выключатели: S1–S9	20–26
Св	светильники: Св1**, Св2**, Св3, Св4, Св5**, Св6–Св8, Св9**, Св10–Св12, Св16	20–26
ИП	извещатели: ИП1–ИП3	20–26
ТВ	розетки ТВ: ТВ1	20–26
LAN	розетки компьютерные: LAN1, LAN2	20–26
БП	блоки питания LED: БП1, БП2	20–26
КУП	электроустановочные изделия: КУП1	20–26
ЩК, ЩС**	щиты: ЩК, ЩС**	20–26
ДФ	домофон: ДФ1	20–26
Ст В1, Ст К1, Ст Т3	стояки (системы В1, Т3, К1): Ст В1-1, Ст К1-1, Ст Т3-1	29–38
Ш	шахты и короба: Ш1	14–16

Марки позиций альбома по видам (продолжение)

Префикс	Что обозначает, позиции	Листы
О	марки отделки (реестр альбома): О1–О10	2–5, 59–80
К, КМ	позиции колерной карты: К1–К9, КМ1–КМ3	49, 50
Р	радиаторы отопления: Р-1–Р-3	27, 28

Примечания

1. Марка отделки О — одна на весь альбом: одна и та же отделка (материал, изделие, цвет, формат) на всех листах имеет одну марку; на развёртках и планах стоят марки этого реестра.
2. Столбец «Колер. карта» — позиции колерной карты (лист 49): К — окраска по коду цвета, КМ — материал без кода цвета; «Помещения» — номера по экспликации; количества — по ведомости отделки помещений (лист 48).
3. Марки позиций: один префикс — один вид позиций на весь альбом (двери Д, окна ОК, мебель М, сантехприборы П, декор ДК, текстиль Т, колерная карта К и КМ, радиаторы РО, розетки Р, выключатели S, светильники Св; стояки — «Ст» и система, например «Ст К1-1»). Совпадение префиксов у разных видов — замечание к исходным данным, при выпуске исправляется в модели.

Допущения и предложения на листе

Основа листа: размеры сняты с плана заказчика, контрольный обмер не выполнен (К-5); высота потолка 2700 мм принята: на плане заказчика не указана (К-5); подрайон климата не задан — принят не северный (жилые от 2,5 м) (К-4); толщины стен приняты: наружные 250 мм, перегородки 120 мм — не обмерены (К-5); разрешённая мощность 15 кВт принята по типовой квартире, технических условий нет (К-6).

Знак «**» — предложение проектировщика, заказчиком не утверждено (согласовать с заказчиком): Св2 — общий свет зоны гостиной над журнальным столом М21 (трек шёл вдоль края стола М3 по проходу); трековая система 4 × 950 лм: поток принят до нормы освещённости, модель и паспорт не выбраны; Св5 — трековая система 2 × 900 лм: светильник добавлен проектировщиком, поток принят до нормы освещённости, модель и паспорт не выбраны; Св1 — подвес висел над проходом без заданной высоты, а стол — без света над ним: подвес по оси стола М3; Св9 — свет у зеркала — над зеркалом у умывальника по его оси (свет на лицо, а не над сантехникой); ЩС — щит слаботочный: место и состав; пол пом. 1, 2, 6 — артикул изделия не выбран: позиция описана характеристиками («аналог по характеристикам»), артикул выбирается при закупке; ИЗ-2: М1 — Было offset 1300…3500: торец дивана в 500 мм от стены В, правые 350 мм проёма Д-2 (3900…4800) упирались в диван; М22 — Было х 4250 — место занял диван М1 (х 4450…5400 от у 1000); К-2: П1 — ванна 1500 вместо 1600 — не заходит в проход перед проёмом Д-4; перед ванной 680 мм — глубина помещения; П3 — умывальник у стены В справа от ванны — перед ним свободно 750 мм, до стены Б 90 мм; К-7: М11 — место стиральной машины: вместо модуля с ящиками 400 справа от варочной; ряд до 3420, журнальный стол М21 (с х 3440) не мешает загрузке; П6 — стиральная машина на кухне: в ванной и санузле места нет; подвод ХВС с шаровым краном, слив — встраиваемый сифон с обратным клапаном (водяной затвор), отдельная группа 6 щита с УЗО 30 мА; Р20 — питание стиральной машины П6 — отдельная группа 6 (УЗО 30 мА); над столешницей в габарите машины, не за корпусом.

См. лист открытых вопросов (лист 6, записи К-2, К-4–К-7; лист 7, запись ИЗ-2).

Изм.	Кол.уч	Лист	№ док.	Подп.	Дата
Разраб.		Кырлан А.С.			04.11.26
Пров.					
ГИП					
Н. контр.					
Утв.					

ГД-2026-006-АИ

Квартира 58 м²

Общая площадь 55,23* м² · * размеры приняты, не замерены (реестр — л. 6, 7, К-5)

Дизайн-проект интерьера

Стадия	Лист	Листов
РП	59	87

Реестр марок отделки и позиций альбома

М б/м

Кырлан Александр Сергеевич

выпуск 04.11.2026 № 94e55e632e · стр. 67 из 96

Схема расположения развёрток и узлов

План квартиры: марки развёрток по помещениям, выноски узлов, ведомость «марка → лист»



Развёртки и узлы: марка → лист

Марка	Помещение / узел	Лист
В	Кухня-гостиная (пом. 1)	61, 62
А	Кухня-гостиная (пом. 1)	63
Б	Кухня-гостиная (пом. 1)	64
Г	Кухня-гостиная (пом. 1)	65
А	Спальня (пом. 2)	66
Б	Спальня (пом. 2)	67, 68
В	Спальня (пом. 2)	69
А, Б, В	Ванная (пом. 3)	70, 71
Г	Ванная (пом. 3)	72
А, Б, В	Санузел (пом. 4)	73
Г	Санузел (пом. 4)	74
А, Б	Прихожая (пом. 5)	75
В, Г	Прихожая (пом. 5)	76, 77
А, Б	Гардеробная (пом. 6)	78
Г	Гардеробная (пом. 6)	79
узел 1	Порог 15 мм: мокрая зона — смежное помещение	80
узел 2	Дверь скрытого монтажа в плоскости стены, плинтус	80
узел 3	Короб стояков К1-1 с люком и звукоизоляцией	80
узел 4	Гидроизоляция санузла: заход на стены 200 мм, примыкание ванны	80
узел 5	Плинтус МДФ 110×16 мм у окрашенной стены по доске (ламинату)	80
узел 6	Плинтус МДФ 110×16 мм у окрашенной стены по керамограниту (плитке)	80

Условные обозначения

- А — марка развёртки: буква стены, стрелка — взгляд
- выноска узла: над полкой — узел, под полкой — лист
- 1 — номер помещения, площадь м²

1000 мм · печать 1:1

Примечания

1. Развёртки — вид на стену изнутри помещения; буквы стен — одна система на весь альбом (как на листах выводов, плитки и отделки).
2. Стены без электроточек, мебели, декора и акцентной отделки развёрток не имеют: их отделка — по ведомости отделки помещений.
3. Узлы — на листе узлов; места применения — по выноскам этого листа и ведомости «марка → лист».

Допущения и предложения на листе

Основа листа: размеры сняты с плана заказчика, контрольный обмер не выполнен (К-5); высота потолка 2700 мм принята: на плане заказчика не указана (К-5); подрайон климата не задан — принят не северный (жилые от 2,5 м) (К-4); толщины стен приняты: наружные 250 мм, перегородки 120 мм — не обмерены (К-5); разрешённая мощность 15 кВт принята по типовой квартире, технических условий нет (К-6).
См. лист открытых вопросов (лист 6, записи К-4–К-6).

Изм.	Кол.уч	Лист	№ док.	Подп.	Дата
Разраб.		Кырлан А.С.			04.11.26
Пров.					
ГИП					
Н. контр.					
Утв.					

ГД-2026-006-АИ

Квартира 58 м²

Общая площадь 55,23* м² · * размеры приняты, не замерены (реестр — л. 6, 7, К-5)

Дизайн-проект интерьера

Стадия	Лист	Листов
РП	60	87

Схема расположения развёрток и узлов

М 1:50

Кырлан Александр Сергеевич


выпуск 04.11.2026 № 94e55e632e · стр. 68 из 96

Развёртка стены В. Кухня-гостиная (пом. 1), кухонный фронт

Кухня-гостиная (пом. 1) · вид изнутри помещения · размеры в мм, отметки в м


ПРЕДВАРИТЕЛЬНО · не для производства работ · открыто пунктов: 10 (реестр — л. 6, 7)

Развёртка стены В

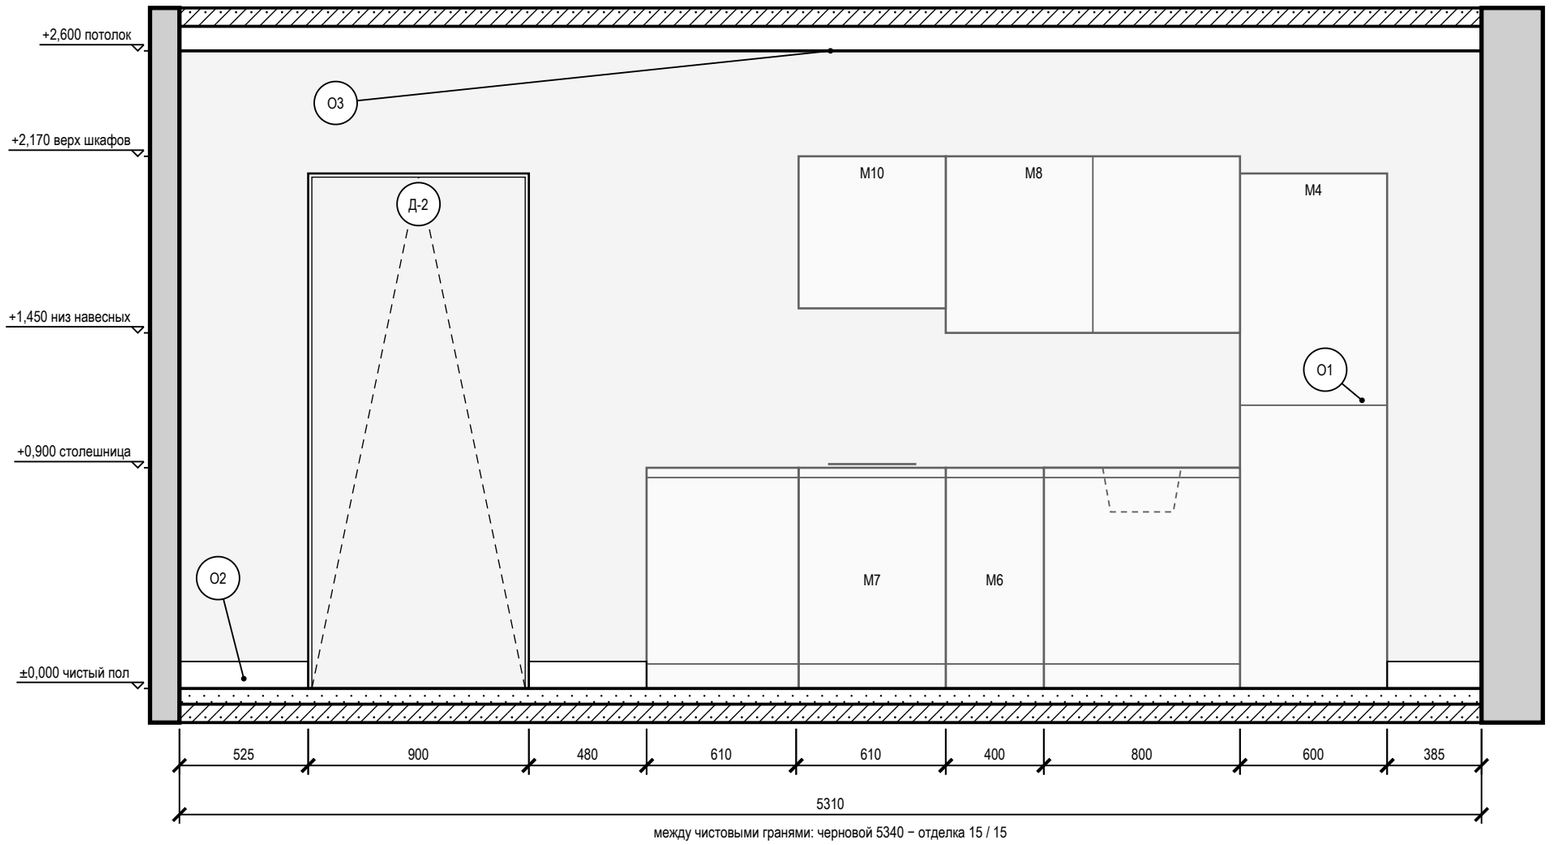

между чистовыми гранями: черновой 5340 − отделка 15 / 15

Схема развёрток (М 1:100)

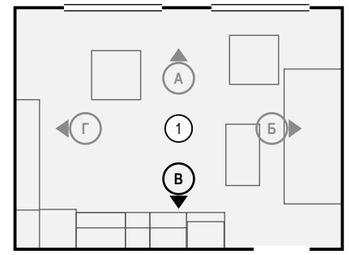

Условные обозначения

- мебель и приборы — фасад по расстановке (условно)
- дверь скрытого монтажа: полотно в плоскости стены (узел — на листе узлов)
- стены и перекрытия в сечении
- О1 — марка отделки по реестру отделки альбома
- А — марка развёртки: буква стены, стрелка — взгляд

Ведомость отделки (на листе)

Марка	Поверхность	Материал, изделие	Цвет, код	Кол.
О1	стены	окраска, Tikkurila, шелковисто-матовая, подготовка Q3	NCS S 1002-Y50R	11,9 м²
О2	плинтус	плинтус МДФ, Orac Decor Luxxus, h 110 мм, SX184, шелковисто-матовая	NCS S 0300-N	1,4 м
О3	потолок	окраска, Tikkurila, глубокоматовая	NCS S 0300-N	21 м²

Примечания

1. Развёртки — вид на стену изнутри помещения, по часовой стрелке; расположение — на схеме листа и на листе 60; размеры — в мм по чистовым поверхностям; отметки — в м от ±0,000; высоты Н — от чистого пола помещения до оси изделия, у декора — до центра.
2. Стена В показана двумя видами: здесь — архитектурная развёртка (мебель, отделка, проёмы, высоты), электроточки и выводы ВК с привязками и таблицей — на листе 62 («Привязки»).
3. Схема мебели, приборов и декора не является технической документацией для производства мебели; габариты — по паспортам изделий.
4. Двери скрытого монтажа — полотно в плоскости стены, отделка стены по полотну, плинтус прерывается у короба (узел — на листе узлов).
5. Потолок — у каждой стены свой, по плану потолков (ПТ2); ступени — зоной, кромка короба перед нишей — тонкой линией; в поле потолка: ПТ1 +2,550.

Допущения и предложения на листе

Основа листа: размеры сняты с плана заказчика, контрольный обмер не выполнен (К-5); высота потолка 2700 мм принята: на плане заказчика не указана (К-5); подрайон климата не задан — принят не северный (жилые от 2,5 м) (К-4); толщины стен приняты: наружные 250 мм, перегородки 120 мм — не обмерены (К-5); разрешённая мощность 15 кВт принята по типовой квартире, технических условий нет (К-6).
См. лист открытых вопросов (лист 6, записи К-4–К-6).

1000 мм · печать 1:1

Изм.	Кол.уч	Лист	№ док.	Подп.	Дата
Разраб.		Кырлан А.С.			04.11.26
Пров.					
ГИП					
Н. контр.					
Утв.					

ГД-2026-006-АИ

Квартира 58 м²

Общая площадь 55,23* м² · * размеры приняты, не замерены (реестр — л. 6, 7, К-5)

Дизайн-проект интерьера

Стадия	Лист	Листов
РП	61	87

Развёртка стены В. Кухня-гостиная (пом. 1), кухонный фронт
М 1:25

Кырлан Александр Сергеевич


выпуск 04.11.2026 № 94e55e632e · стр. 69 из 96

Привязки электроточек и выводов ВК, стена В. Кухня-гостиная (пом. 1)

Кухня-гостиная (пом. 1) · вид изнутри помещения · привязки в мм, отметки в м · к развёртке на листе 61

ПРЕДВАРИТЕЛЬНО · не для производства работ · открыто пунктов: 10 (реестр — л. 6, 7)

Развёртка стены В: электроточки и выводы

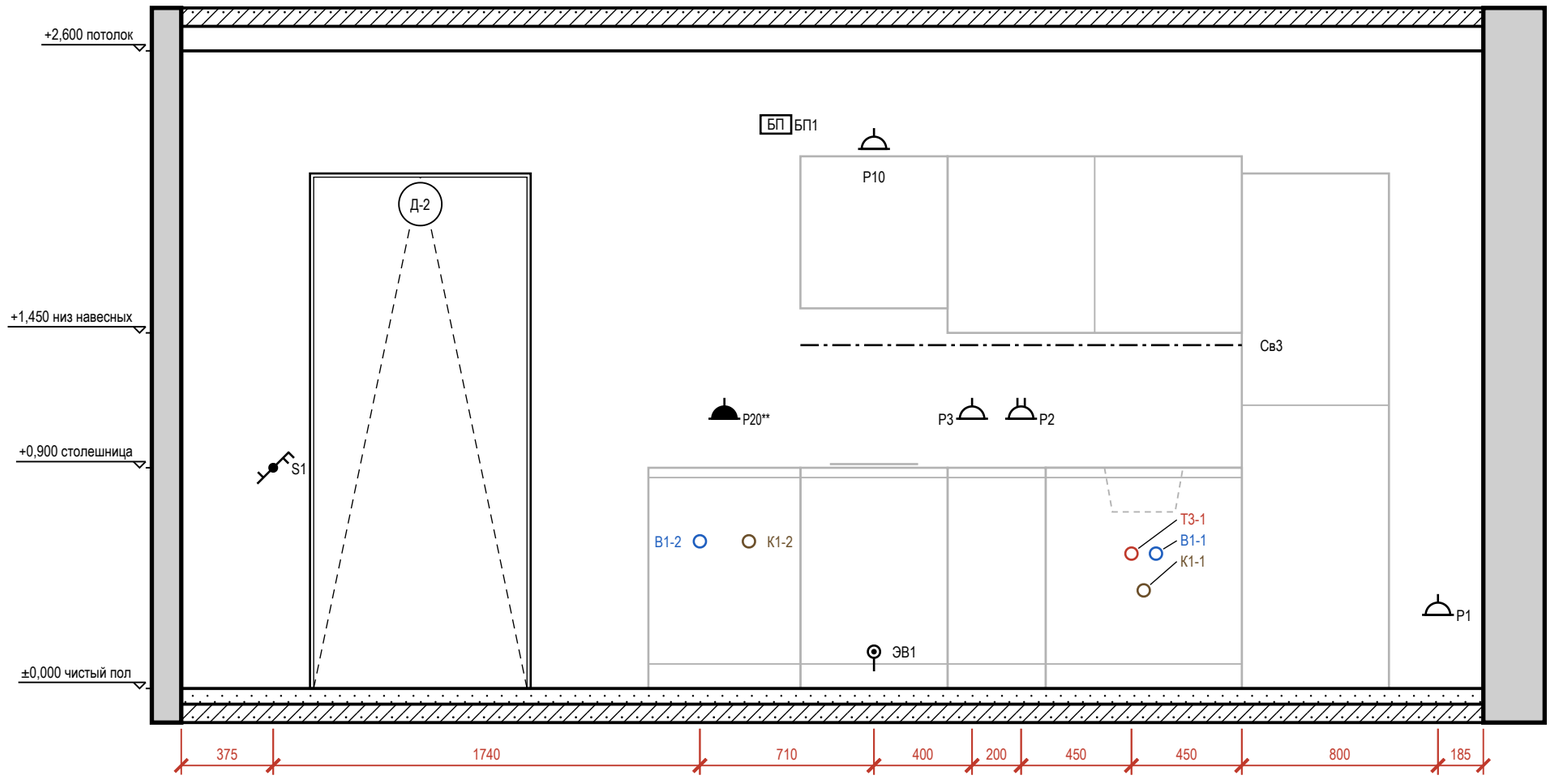

Условные обозначения

- розетка с заземляющим контактом; у знака — марка, ×N постов в рамке, гр. — группа щита, H — высота оси, мм
- розетка влагозащищённая IP44
- вывод кабеля для подключения прибора (без розетки), марка ЭВ
- выключатель одноклавишный
- выключатель двухклавишный (флажков — по числу клавиш)
- выключатель с проходной или перекрёстной клавишей (обратный флажок); тип клавиши — в подписи
- светодиодная лента в профиле / в карнизе короба
- БП — блок питания LED, с доступом (люк от 100×100 мм)
- вывод В1 (код — в ведомости привязок)
- вывод Т3 (код — в ведомости привязок)
- вывод К1 (код — в ведомости привязок)
- привязки точек и выводов от угла и от пола, мм
- А — марка развёртки: буква стены, стрелка — взгляд

Схема развёрток (М 1:100)

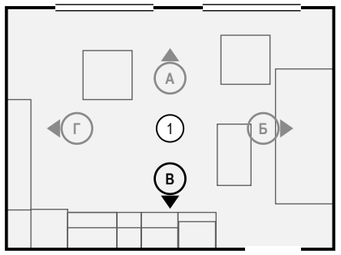


Таблица привязок электроточек и выводов

Марка	Назначение	От угла, мм	H от пола, мм	Примечание
S1	выключатель	375	900	гр. 1
В1-2	холодная вода — стиральная машина	2115	600	кран машины
Р20**	розетка: стиральная машина	2215	1100	гр. 6, IP44
К1-2	канализация — стиральная машина	2315	600	Ø40
БП1	блок питания LED	2425	2300	гр. 1
ЭВ1	вывод кабеля: варочная панель	2825	150	гр. 3
Р10	розетка: вытяжка (встроена в дно М10)	2825	2200	гр. 2

Марка	Назначение	От угла, мм	H от пола, мм	Примечание
Р3	розетка: рабочая зона	3225	1100	гр. 2
Р2	розетка: рабочая зона	3425	1100	рамка 2 поста, гр. 2
Т3-1	горячая вода — мойка кухонная	3875	550	межос. 100
К1-1	канализация — мойка кухонная	3925	400	Ø50
В1-1	холодная вода — мойка кухонная	3975	550	межос. 100
Св3	светильник настенный	4325	1400	гр. 1, лента 2525–4325 от угла
Р1	розетка: холодильник	5125	300	гр. 2

Допущения и предложения на листе

Основа листа: размеры сняты с плана заказчика, контрольный обмер не выполнен (К-5); высота потолка 2700 мм принята: на плане заказчика не указана (К-5); подрайон климата не задан — принят не северный (жилые от 2,5 м) (К-4); толщины стен приняты: наружные 250 мм, перегородки 120 мм — не обмерены (К-5); разрешённая мощность 15 кВт принята по типовой квартире, технических условий нет (К-6).

Знак «**» — предложение проектировщика, заказчиком не утверждено (согласовать с заказчиком): К-7: Р20 — питание стиральной машины П6 — отдельная группа 6 (УЗО 30 мА); над столешницей в габарите машины, не за корпусом.

См. лист открытых вопросов (лист 6, записи К-4–К-7).

Примечания

1. Вид «Привязки» стены В — электроточки и выводы ВК; архитектурная развёртка (мебель, отделка, проёмы, высоты) — на листе 61, расположение — на листе 60. Мебель и приборы — подложкой для ориентира; их марки и обозначения мебели, проёмов и стен — там же.
2. Привязки — в мм: по горизонтали от левого чистового угла стены до оси изделия, H — от чистого пола до оси; все точки — в таблице привязок. Красная цепочка — привязки по осям; точки ближе 150 мм одна к другой в цепочку не дробятся — их привязки только в таблице.
3. У знака — марка электроточки (Р — розетка, S — выключатель, Св — светильник, ЭВ — вывод кабеля); посты в рамке и группа щита — в графе «Примечание»; группы по клавишам выключателя — на листе выключателей.
4. Коды выводов ВК: В1 — холодная вода, Т3 — горячая вода, К1 — канализация; номер после дефиса — номер вывода на листе выводов сантехники.
5. Выводы кухонной техники — по утверждённому проекту кухни: привязки выводов даются от осей модулей гарнитура.

1000 мм · печать 1:1

Изм.	Кол.уч	Лист	№ док.	Подп.	Дата
Разраб.		Кырлан А.С.			04.11.26
Пров.					
ГИП					
Н. контр.					
Утв.					

ГД-2026-006-АИ

Квартира 58 м²

Общая площадь 55,23* м² · * размеры приняты, не замерены (реестр — л. 6, 7, К-5)

Дизайн-проект интерьера

Стадия	Лист	Листов
РП	62	87

Привязки электроточек и выводов ВК, стена В. Кухня-гостиная (пом. 1)

М 1:25

Кырлан Александр Сергеевич


выпуск 04.11.2026 № 94e55e632e · стр. 70 из 96

Развёртка стены А. Кухня-гостиная (пом. 1)

Кухня-гостиная (пом. 1) · вид изнутри помещения · размеры в мм, отметки в м


ПРЕДВАРИТЕЛЬНО · не для производства работ · открыто пунктов: 10 (реестр — л. 6, 7)

Развёртка стены А

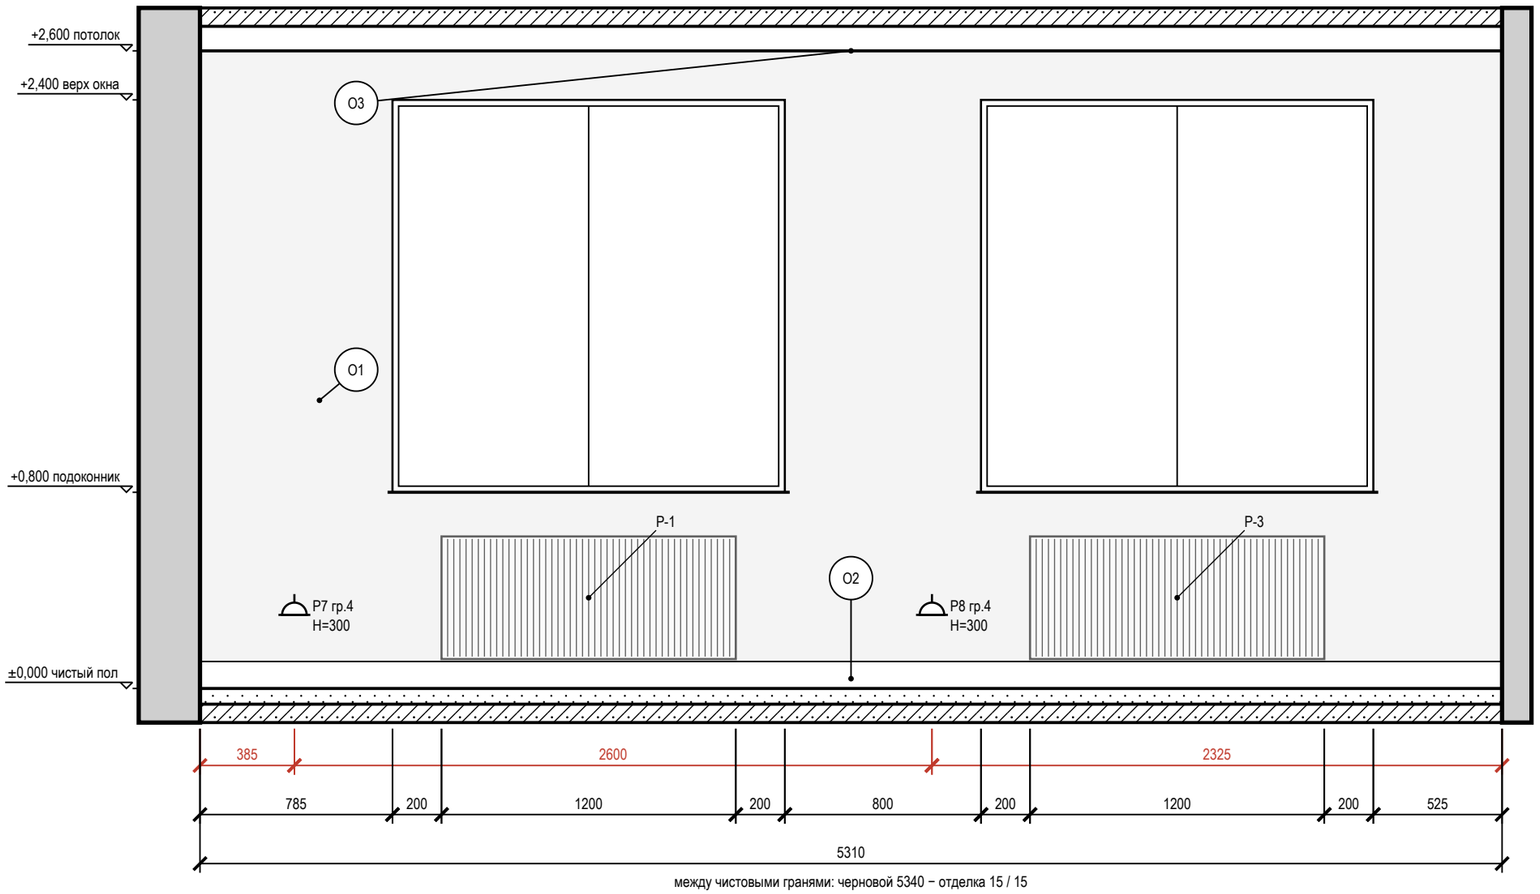

между чистовыми гранями: черновой 5340 − отделка 15 / 15

Схема развёрток (М 1:100)

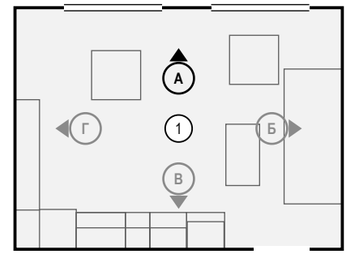

Условные обозначения

- розетка с заземляющим контактом; у знака — марка, ×N постов в рамке, гр. — группа щита, Н — высота оси, мм
- привязки точек и выводов от угла и от пола, мм
- мебель и приборы — фасад по расстановке (условно)
- окно: проём, рама, подоконник
- радиатор отопления; марка — по плану отопления
- стены и перекрытия в сечении
- О1 — марка отделки по реестру отделки альбома
- А — марка развёртки: буква стены, стрелка — взгляд

Ведомость отделки (на листе)

Марка	Поверхность	Материал, изделие	Цвет, код	Кол.
О1	стены	окраска, Tikkurila, шелковисто-матовая, подготовка Q3	NCS S 1002-Y50R	8,7 м²
О2	плинтус	плинтус МДФ, Orac Decor Luxxus, h 110 мм, SX184, шелковисто-матовая	NCS S 0300-N	5,3 м
О3	потолок	окраска, Tikkurila, глубокоматовая	NCS S 0300-N	21 м²

Допущения и предложения на листе

Основа листа: размеры сняты с плана заказчика, контрольный обмер не выполнен (К-5); высота потолка 2700 мм принята: на плане заказчика не указана (К-5); подрайон климата не задан — принят не северный (жилые от 2,5 м) (К-4); толщины стен приняты: наружные 250 мм, перегородки 120 мм — не обмерены (К-5); разрешённая мощность 15 кВт принята по типовой квартире, технических условий нет (К-6).

См. лист открытых вопросов (лист 6, записи К-4–К-6).

Примечания

1. Развёртки — вид на стену изнутри помещения, по часовой стрелке; расположение — на схеме листа и на листе 60; размеры — в мм по чистовым поверхностям; отметки — в м от ±0,000; высоты Н — от чистого пола помещения до оси изделия, у декора — до центра.
2. Красная цепочка — привязки электроточек и выводов по осям от угла чистовых стен; высота Н — у знака, от чистого пола до оси; высоты мебели, проёмов и границ отделки — колонкой отметок слева. Стена с 5 и более точками или с мелкими звеньями привязок показана двумя видами: архитектурная развёртка (мебель, отделка, проёмы, высоты) и вид «Привязки» на отдельном листе — точки и выводы с марками, одна цепочка по осям и таблица привязок (каждая точка — строка).
3. У знака электроточки: марка (Р — розетка, S — выключатель, Св — светильник, ЭВ — вывод кабеля), ×N — число постов в рамке, гр. — группа щита, Н — высота оси от чистого пола, мм; группы по клавишам выключателя — на листе выключателей.
4. Схема мебели, приборов и декора не является технической документацией для производства мебели; габариты — по паспортам изделий.
5. Потолок — у каждой стены свой, по плану потолков (ПТ2); ступени — зоной, кромка короба перед нишей — тонкой линией; в поле потолка: ПТ1 +2,550.

1000 мм · печать 1:1

Изм.	Кол.уч	Лист	№ док.	Подп.	Дата
Разраб.		Кырлан А.С.			04.11.26
Пров.					
ГИП					
Н. контр.					
Утв.					

ГД-2026-006-АИ

Квартира 58 м²

Общая площадь 55,23* м² · * размеры приняты, не замерены (реестр — л. 6, 7, К-5)

Дизайн-проект интерьера

Стадия	Лист	Листов
РП	63	87

Развёртка стены А. Кухня-гостиная (пом. 1)

М 1:25

Кырлан Александр Сергеевич


выпуск 04.11.2026 № 94e55e632e · стр. 71 из 96

Развёртка стены Б. Кухня-гостиная (пом. 1)

Кухня-гостиная (пом. 1) · вид изнутри помещения · размеры в мм, отметки в м

ПРЕДВАРИТЕЛЬНО · не для производства работ · открыто пунктов: 10 (реестр — л. 6, 7)

Развёртка стены Б

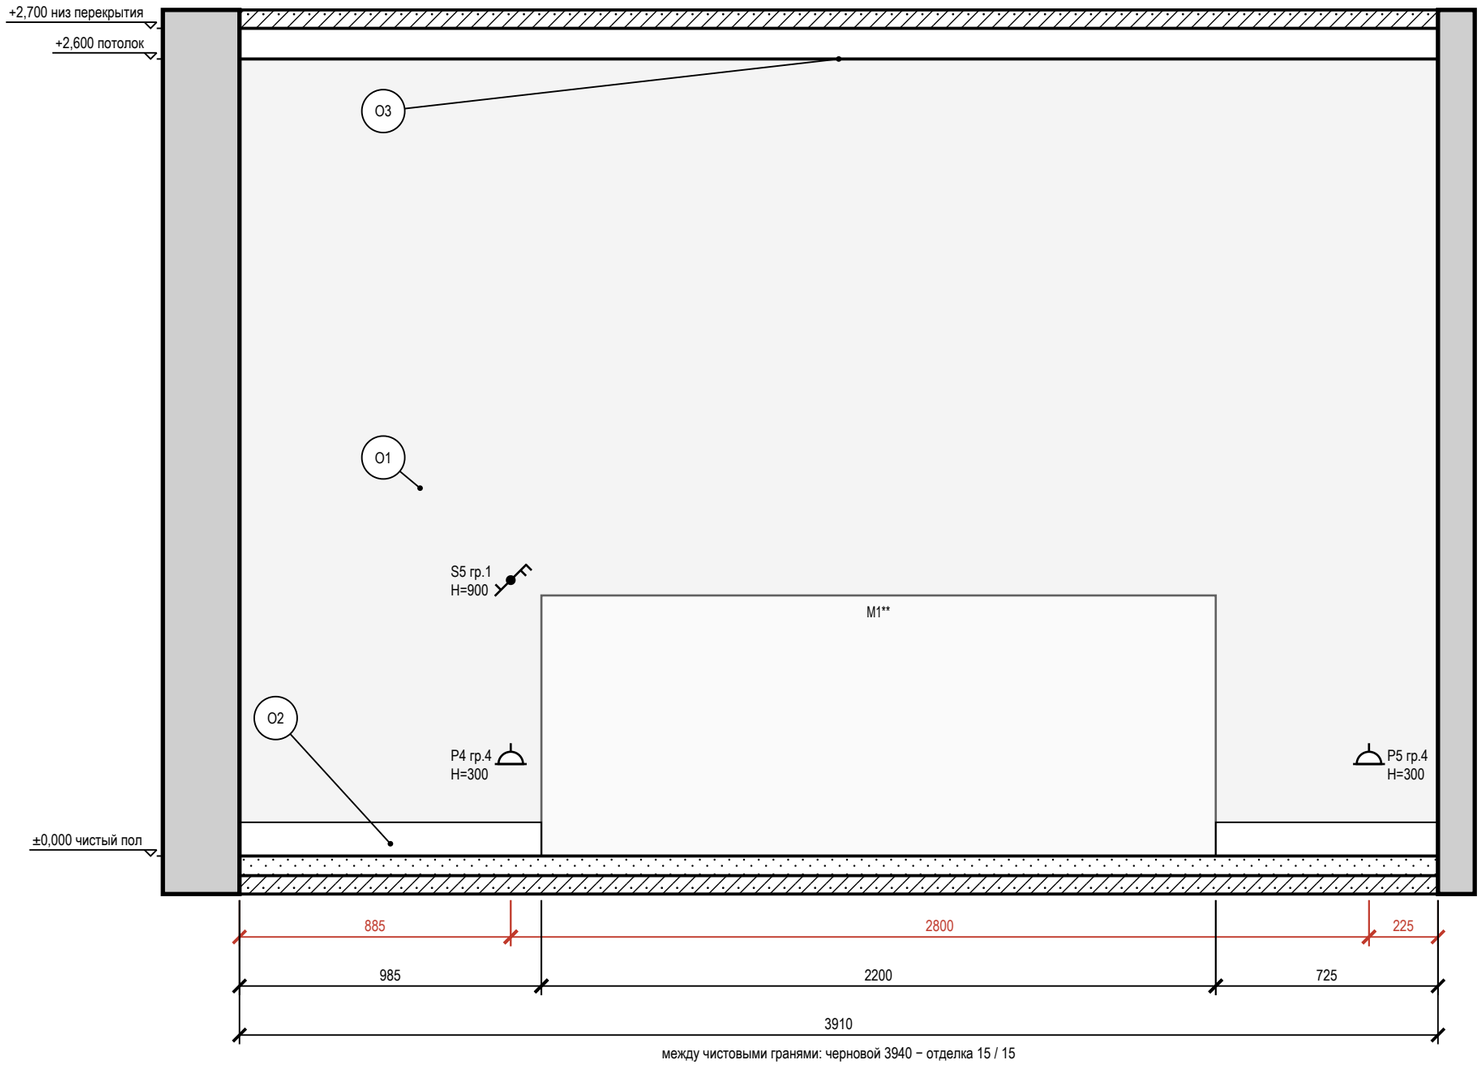

между чистовыми гранями: черновой 3940 − отделка 15 / 15

Допущения и предложения на листе

Основа листа: размеры сняты с плана заказчика, контрольный обмер не выполнен (К-5); высота потолка 2700 мм принята: на плане заказчика не указана (К-5); подрайон климата не задан — принят не северный (жилые от 2,5 м) (К-4); толщины стен приняты: наружные 250 мм, перегородки 120 мм — не обмерены (К-5); разрешённая мощность 15 кВт принята по типовой квартире, технических условий нет (К-6).

Знак «**» — предложение проектировщика, заказчиком не утверждено (согласовать с заказчиком): И3-2: М1 — Было offset 1300…3500: торец дивана в 500 мм от стены В, правые 350 мм проёма Д-2 (3900…4800) упирались в диван.


См. лист открытых вопросов (лист 6, записи К-4–К-6; лист 7, запись И3-2).

Примечания

1. Развёртки — вид на стену изнутри помещения, по часовой стрелке; расположение — на схеме листа и на листе 60; размеры — в мм по чистовым поверхностям; отметки — в м от ±0,000; высоты Н — от чистого пола помещения до оси изделия, у декора — до центра.
2. Красная цепочка — привязки электроточек и выводов по осям от угла чистовых стен; высота Н — у знака, от чистого пола до оси; высоты мебели, проёмов и границ отделки — колонкой отметок слева. Стена с 5 и более точками или с мелкими звеньями привязок показана двумя видами: архитектурная развёртка (мебель, отделка, проёмы, высоты) и вид «Привязки» на отдельном листе — точки и выводы с марками, одна цепочка по осям и таблица привязок (каждая точка — строка).
3. У знака электроточки: марка (Р — розетка, S — выключатель, Св — светильник, ЭВ — вывод кабеля), ×N — число постов в рамке, гр. — группа щита, Н — высота оси от чистого пола, мм; группы по клавишам выключателя — на листе выключателей.
4. Схема мебели, приборов и декора не является технической документацией для производства мебели; габариты — по паспортам изделий.
5. Потолок — у каждой стены свой, по плану потолков (ПТ2); ступени — зоной, кромка короба перед нишей — тонкой линией; в поле потолка: ПТ1 +2,550.

1000 мм · печать 1:1

Схема развёрток (М 1:100)

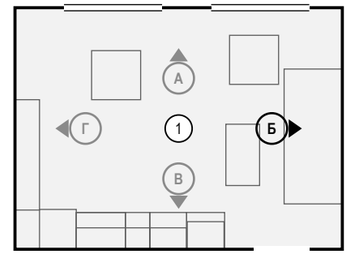

Условные обозначения

- розетка с заземляющим контактом; у знака — марка, ×N постов в рамке, гр. — группа щита, Н — высота оси, мм
- выключатель одноклавишный
- выключатель двухклавишный (флажков — по числу клавиш)
- выключатель с проходной или перекрёстной клавишей (обратный флажок); тип клавиши — в подписи
- привязки точек и выводов от угла и от пола, мм
- мебель и приборы — фасад по расстановке (условно)
- стены и перекрытия в сечении
- О1 — марка отделки по реестру отделки альбома
- А — марка развёртки: буква стены, стрелка — взгляд

Ведомость отделки (на листе)

Марка	Поверхность	Материал, изделие	Цвет, код	Кол.
О1	стены	окраска, Tikkurila, шелковисто-матовая, подготовка Q3	NCS S 1002-Y50R	10,2 м²
О2	плинтус	плинтус МДФ, Orac Decor Luxxus, h 110 мм, SX184, шелковисто-матовая	NCS S 0300-N	1,7 м
О3	потолок	окраска, Tikkurila, глубокоматовая	NCS S 0300-N	21 м²

Изм.	Кол.уч	Лист	№ док.	Подп.	Дата
Разраб.		Кырлан А.С.			04.11.26
Пров.					
ГИП					
Н. контр.					
Утв.					

ГД-2026-006-АИ

Квартира 58 м²

Общая площадь 55,23* м² · * размеры приняты, не замерены (реестр — л. 6, 7, К-5)

Дизайн-проект интерьера

Стадия	Лист	Листов
РП	64	87

Развёртка стены Б. Кухня-гостиная (пом. 1)

М 1:20

Кырлан Александр Сергеевич

выпуск 04.11.2026 № 94e55e632e · стр. 72 из 96

Развёртка стены Г. Кухня-гостиная (пом. 1)

Кухня-гостиная (пом. 1) · вид изнутри помещения · размеры в мм, отметки в м

ПРЕДВАРИТЕЛЬНО · не для производства работ · открыто пунктов: 10 (реестр — л. 6, 7)

Развёртка стены Г


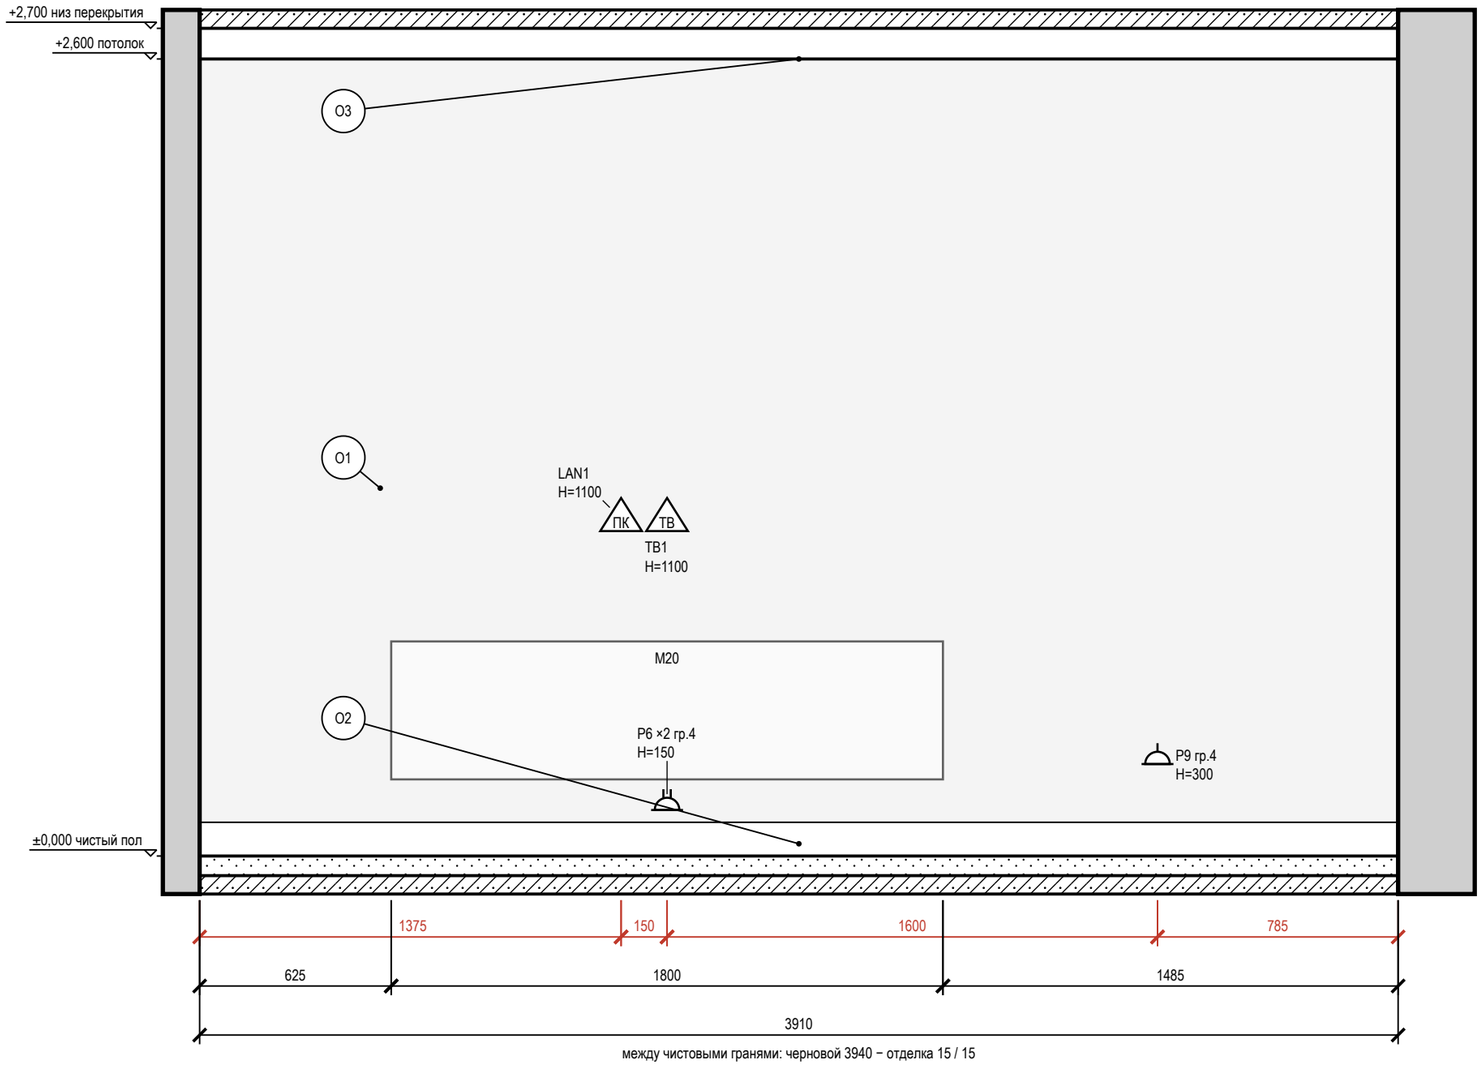


Схема развёрток (М 1:100)

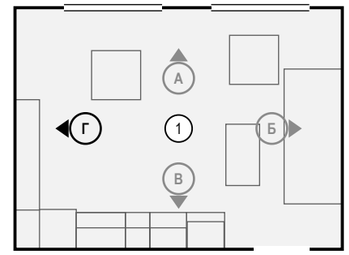

Условные обозначения

- розетка с заземляющим контактом; у знака — марка, ×N постов в рамке, гр. — группа щита, Н — высота оси, мм
- ПК — розетка компьютерная RJ45
- ТВ — розетка телевизионная
- привязки точек и выводов от угла и от пола, мм
- мебель и приборы — фасад по расстановке (условно)
- стены и перекрытия в сечении
- О1 — марка отделки по реестру отделки альбома
- А — марка развёртки: буква стены, стрелка — взгляд

Ведомость отделки (на листе)

Марка	Поверхность	Материал, изделие	Цвет, код	Кол.
О1	стены	окраска, Tikkurila, шелковисто-матовая, подготовка Q3	NCS S 1002-Y50R	10,2 м²
О2	плинтус	плинтус МДФ, Orac Decor Luxxus, h 110 мм, SX184, шелковисто-матовая	NCS S 0300-N	3,9 м
О3	потолок	окраска, Tikkurila, глубокоматовая	NCS S 0300-N	21 м²

Допущения и предложения на листе

Основа листа: размеры сняты с плана заказчика, контрольный обмер не выполнен (К-5); высота потолка 2700 мм принята: на плане заказчика не указана (К-5); подрайон климата не задан — принят не северный (жилые от 2,5 м) (К-4); толщины стен приняты: наружные 250 мм, перегородки 120 мм — не обмерены (К-5); разрешённая мощность 15 кВт принята по типовой квартире, технических условий нет (К-6).

См. лист открытых вопросов (лист 6, записи К-4–К-6).

Примечания

1. Развёртки — вид на стену изнутри помещения, по часовой стрелке; расположение — на схеме листа и на листе 60; размеры — в мм по чистовым поверхностям; отметки — в м от ±0,000; высоты Н — от чистого пола помещения до оси изделия, у декора — до центра.
2. Красная цепочка — привязки электроточек и выводов по осям от угла чистовых стен; высота Н — у знака, от чистого пола до оси; высоты мебели, проёмов и границ отделки — колонкой отметок слева. Стена с 5 и более точками или с мелкими звеньями привязок показана двумя видами: архитектурная развёртка (мебель, отделка, проёмы, высоты) и вид «Привязки» на отдельном листе — точки и выводы с марками, одна цепочка по осям и таблица привязок (каждая точка — строка).
3. У знака электроточки: марка (Р — розетка, S — выключатель, Св — светильник, ЭВ — вывод кабеля), ×N — число постов в рамке, гр. — группа щита, Н — высота оси от чистого пола, мм; группы по клавишам выключателя — на листе выключателей.
4. Схема мебели, приборов и декора не является технической документацией для производства мебели; габариты — по паспортам изделий.
5. Потолок — у каждой стены свой, по плану потолков (ПТ2); ступени — зоной, кромка короба перед нишей — тонкой линией; в поле потолка: ПТ1 +2,550.

1000 мм · печать 1:1

Изм.	Кол.уч	Лист	№ док.	Подп.	Дата
Разраб.		Кырлан А.С.			04.11.26
Пров.					
ГИП					
Н. контр.					
Утв.					

ГД-2026-006-АИ

Квартира 58 м²

Общая площадь 55,23* м² · * размеры приняты, не замерены (реестр — л. 6, 7, К-5)

Дизайн-проект интерьера

Стадия	Лист	Листов
РП	65	87

Развёртка стены Г. Кухня-гостиная (пом. 1)

М 1:20

Кырлан Александр Сергеевич


выпуск 04.11.2026 № 94e55e632e · стр. 73 из 96

Развёртка стены А. Спальня (пом. 2)

Спальня (пом. 2) · вид изнутри помещения · размеры в мм, отметки в м


ПРЕДВАРИТЕЛЬНО · не для производства работ · открыто пунктов: 10 (реестр — л. 6, 7)

Развёртка стены А

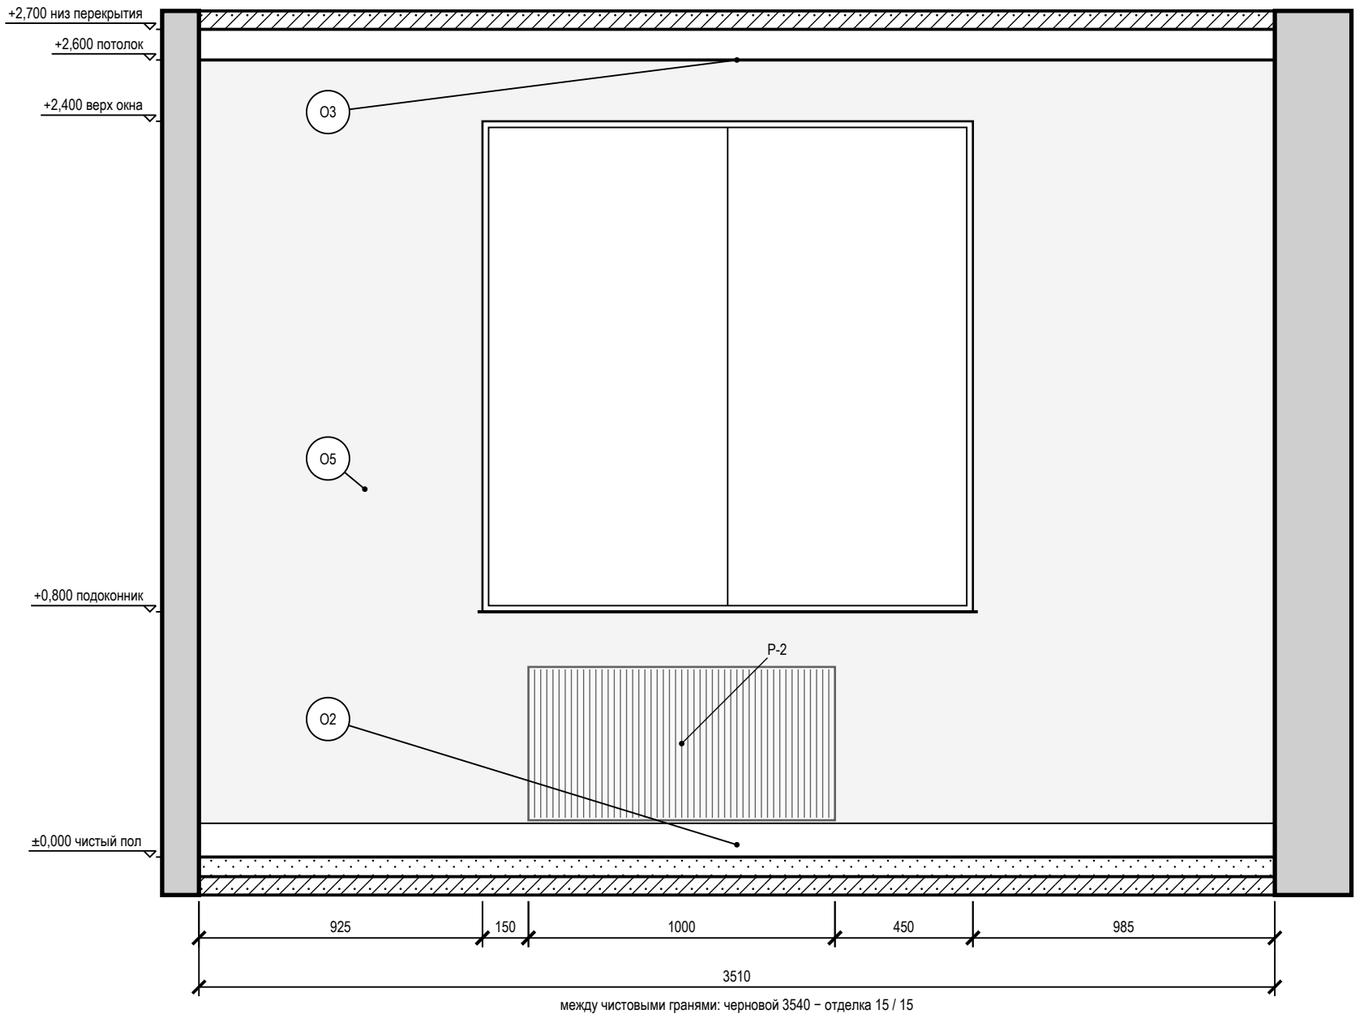

между чистовыми гранями: черновой 3540 − отделка 15 / 15

Схема развёрток (М 1:100)

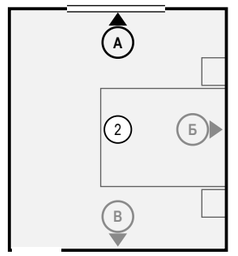

Условные обозначения

- мебель и приборы — фасад по расстановке (условно)
- окно: проём, рама, подоконник
- радиатор отопления; марка — по плану отопления
- стены и перекрытия в сечении
- О1 — марка отделки по реестру отделки альбома
- А — марка развёртки: буква стены, стрелка — взгляд

Ведомость отделки (на листе)

Марка	Поверхность	Материал, изделие	Цвет, код	Кол.
О2	плинтус	плинтус МДФ, Orac Decor Luxxus, h 110 мм, SX184, шелковисто-матовая	NCS S 0300-N	3,5 м
О3	потолок	окраска, Tikkurila, глубокоматовая	NCS S 0300-N	13,9 м²
О5	стены	окраска, Tikkurila, глубокоматовая, подготовка Q3	NCS S 1502-Y50R	6,6 м²

Примечания

1. Развёртки — вид на стену изнутри помещения, по часовой стрелке; расположение — на схеме листа и на листе 60; размеры — в мм по чистовым поверхностям; отметки — в м от ±0,000; высоты Н — от чистого пола помещения до оси изделия, у декора — до центра.
2. Схема мебели, приборов и декора не является технической документацией для производства мебели; габариты — по паспортам изделий.
3. Потолок — у каждой стены свой, по плану потолков (ПТ2); ступени — зоной, кромка короба перед нишей — тонкой линией; в поле потолка: ПТ1 +2,550.

Допущения и предложения на листе

Основа листа: размеры сняты с плана заказчика, контрольный обмер не выполнен (К-5); высота потолка 2700 мм принята: на плане заказчика не указана (К-5); подрайон климата не задан — принят не северный (жилые от 2,5 м) (К-4); толщины стен приняты: наружные 250 мм, перегородки 120 мм — не обмерены (К-5); разрешённая мощность 15 кВт принята по типовой квартире, технических условий нет (К-6).

См. лист открытых вопросов (лист 6, записи К-4–К-6).

1000 мм · печать 1:1

Изм.	Кол.уч	Лист	№ док.	Подп.	Дата
Разраб.		Кырлан А.С.			04.11.26
Пров.					
ГИП					
Н. контр.					
Утв.					

ГД-2026-006-АИ

Квартира 58 м²

Общая площадь 55,23* м² · * размеры приняты, не замерены (реестр — л. 6, 7, К-5)

Дизайн-проект интерьера

Стадия	Лист	Листов
РП	66	87

Развёртка стены А. Спальня (пом. 2)

М 1:20

Кырлан Александр Сергеевич


выпуск 04.11.2026 № 94e55e632e · стр. 74 из 96

Развёртка стены Б. Спальня (пом. 2)

Спальня (пом. 2) · вид изнутри помещения · размеры в мм, отметки в м


ПРЕДВАРИТЕЛЬНО · не для производства работ · открыто пунктов: 10 (реестр — л. 6, 7)

Развёртка стены Б

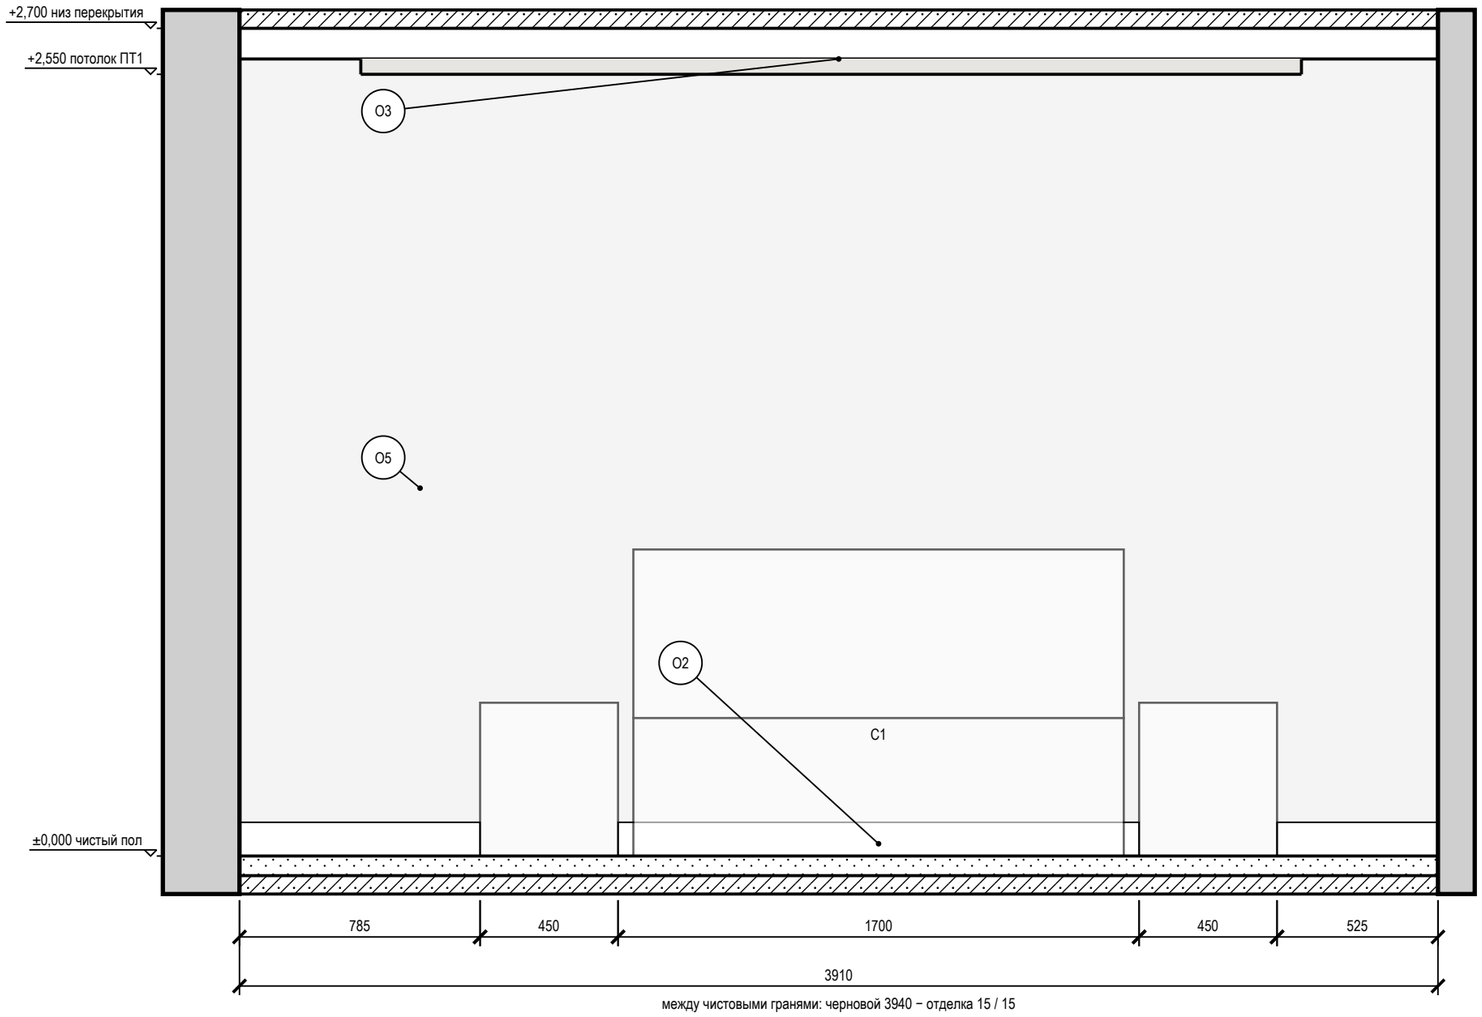

между чистовыми гранями: черновой 3940 − отделка 15 / 15

Схема развёрток (М 1:100)

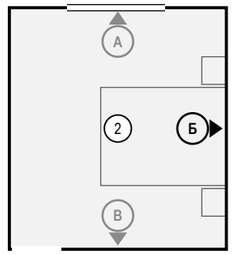

Условные обозначения

- мебель и приборы — фасад по расстановке (условно)
- стены и перекрытия в сечении
- О1 — марка отделки по реестру отделки альбома
- А — марка развёртки: буква стены, стрелка — взгляд

Ведомость отделки (на листе)

Марка	Поверхность	Материал, изделие	Цвет, код	Кол.
О2	плинтус	плинтус МДФ, Orac Decor Luxxus, h 110 мм, SX184, шелковисто-матовая	NCS S 0300-N	3 м
О3	потолок	окраска, Tikkurila, глубокоматовая	NCS S 0300-N	13,9 м²
О5	стены	окраска, Tikkurila, глубокоматовая, подготовка Q3	NCS S 1502-Y50R	10,2 м²

Примечания

1. Развёртки — вид на стену изнутри помещения, по часовой стрелке; расположение — на схеме листа и на листе 60; размеры — в мм по чистовым поверхностям; отметки — в м от ±0,000; высоты Н — от чистого пола помещения до оси изделия, у декора — до центра.
2. Стена Б показана двумя видами: здесь — архитектурная развёртка (мебель, отделка, проёмы, высоты), электроточки и выводы ВК с привязками и таблицей — на листе 68 («Привязки»).
3. Схема мебели, приборов и декора не является технической документацией для производства мебели; габариты — по паспортам изделий.
4. Потолок — у каждой стены свой, по плану потолков (ПТ2, ПТ1); ступени — зоной, кромка короба перед нишей — тонкой линией.

Допущения и предложения на листе

Основа листа: размеры сняты с плана заказчика, контрольный обмер не выполнен (К-5); высота потолка 2700 мм принята: на плане заказчика не указана (К-5); подрайон климата не задан — принят не северный (жилые от 2,5 м) (К-4); толщины стен приняты: наружные 250 мм, перегородки 120 мм — не обмерены (К-5); разрешённая мощность 15 кВт принята по типовой квартире, технических условий нет (К-6).

См. лист открытых вопросов (лист 6, записи К-4–К-6).

1000 мм · печать 1:1

Изм.	Кол.уч	Лист	№ док.	Подп.	Дата
Разраб.		Кырлан А.С.			04.11.26
Пров.					
ГИП					
Н. контр.					
Утв.					

ГД-2026-006-АИ

Квартира 58 м²

Общая площадь 55,23* м² · * размеры приняты, не замерены (реестр — л. 6, 7, К-5)

Дизайн-проект интерьера

Стадия	Лист	Листов
РП	67	87

Развёртка стены Б. Спальня (пом. 2)

М 1:20

Кырлан Александр Сергеевич

выпуск 04.11.2026 № 94e55e632e · стр. 75 из 96

Привязки электроточек, стена Б. Спальня (пом. 2)

Спальня (пом. 2) · вид изнутри помещения · привязки в мм, отметки в м · к развёртке на листе 67

ПРЕДВАРИТЕЛЬНО · не для производства работ · открыто пунктов: 10 (реестр — л. 6, 7)

Развёртка стены Б: электроточки и выводы

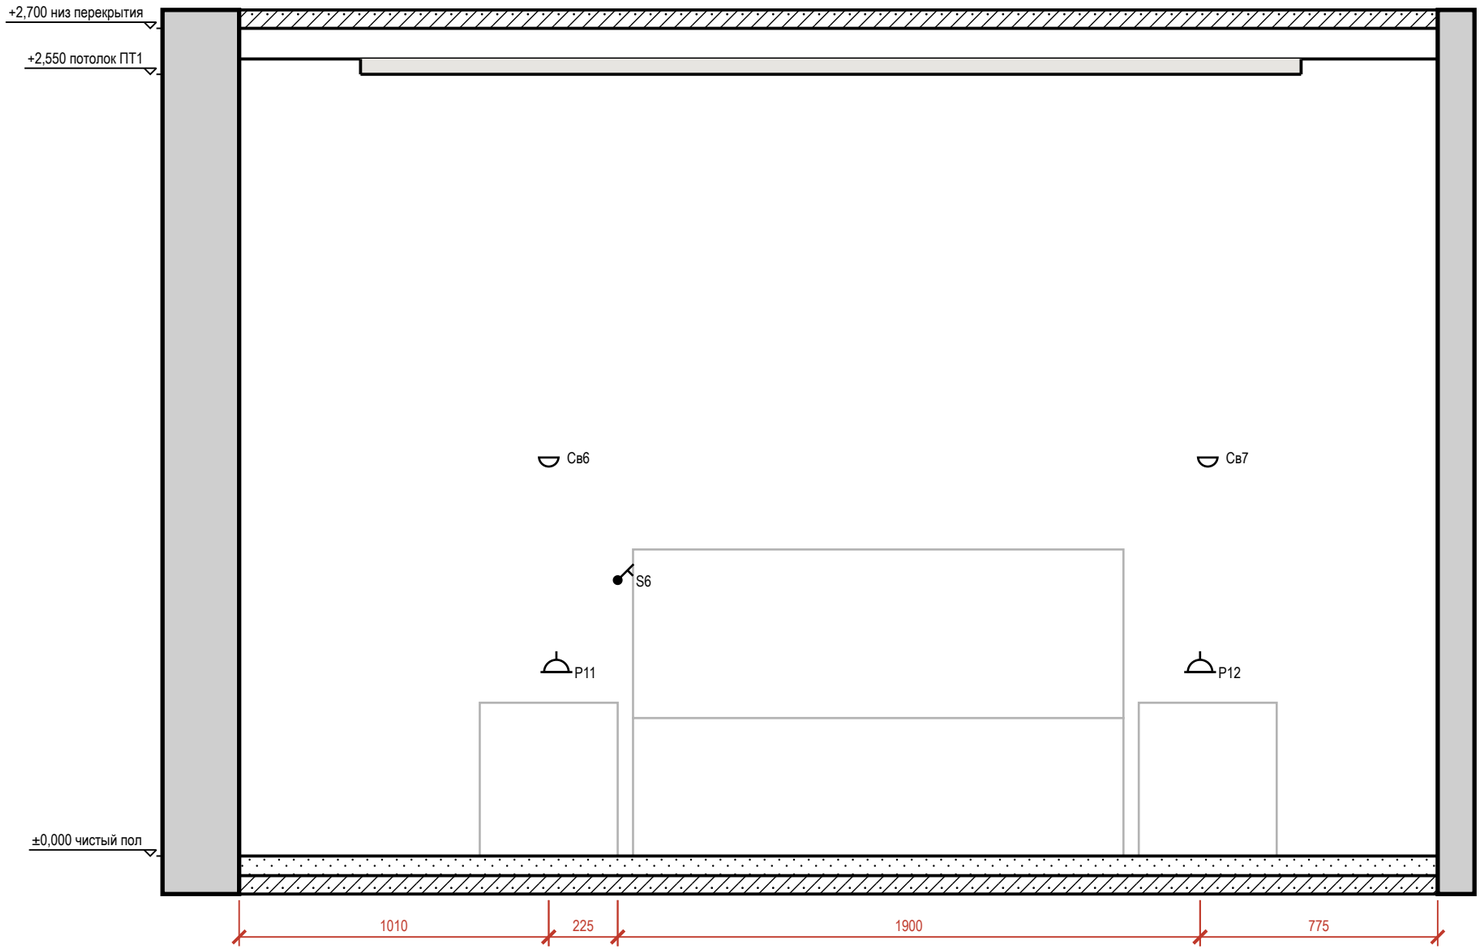



Таблица привязок электроточек и выводов

Марка	Назначение	От угла, мм	Н от пола, мм	Примечание
Св6	светильник настенный	1010	1300	гр. 1
P11	розетка	1035	600	гр. 4
S6	выключатель	1235	900	гр. 1
P12	розетка	3135	600	гр. 4
Св7	светильник настенный	3160	1300	гр. 1

Условные обозначения

- розетка с заземляющим контактом; у знака — марка, ×N постов в рамке, гр. — группа щита, Н — высота оси, мм
- выключатель одноклавишный
- светильник настенный (бра), Н — высота оси
- привязки точек и выводов от угла и от пола, мм
- марка развёртки: буква стены, стрелка — взгляд

Схема развёрток (М 1:50)

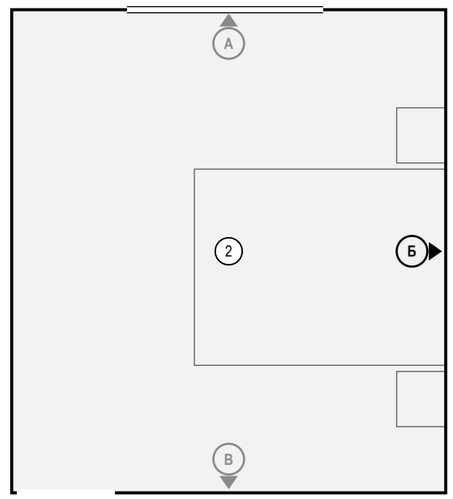

Примечания

1. Вид «Привязки» стены Б — электроточки и выводы ВК; архитектурная развёртка (мебель, отделка, проёмы, высоты) — на листе 67, расположение — на листе 60. Мебель и приборы — подложкой для ориентира; их марки и обозначения мебели, проёмов и стен — там же.
2. Привязки — в мм: по горизонтали от левого чистового угла стены до оси изделия, Н — от чистого пола до оси; все точки — в таблице привязок. Красная цепочка — привязки по осям; точки ближе 120 мм одна к другой в цепочку не дробятся — их привязки только в таблице.
3. У знака — марка электроточки (Р — розетка, S — выключатель, Св — светильник, ЭВ — вывод кабеля); посты в рамке и группа щита — в графе «Примечание»; группы по клавишам выключателя — на листе выключателей.

Допущения и предложения на листе

Основа листа: размеры сняты с плана заказчика, контрольный обмер не выполнен (К-5); высота потолка 2700 мм принята: на плане заказчика не указана (К-5); подрайон климата не задан — принят не северный (жилые от 2,5 м) (К-4); толщины стен приняты: наружные 250 мм, перегородки 120 мм — не обмерены (К-5); разрешённая мощность 15 кВт принята по типовой квартире, технических условий нет (К-6).

См. лист открытых вопросов (лист 6, записи К-4–К-6).

1000 мм · печать 1:1

Изм.	Кол.уч	Лист	№ док.	Подп.	Дата
Разраб.		Кырлан А.С.			04.11.26
Пров.					
ГИП					
Н. контр.					
Утв.					

ГД-2026-006-АИ

Квартира 58 м²

Общая площадь 55,23* м² · * размеры приняты, не замерены (реестр — л. 6, 7, К-5)

Дизайн-проект интерьера

Стадия	Лист	Листов
РП	68	87

Привязки электроточек, стена Б. Спальня (пом. 2)

М 1:20

Кырлан Александр Сергеевич

выпуск 04.11.2026 № 94e55e632e · стр. 76 из 96

Развёртка стены В. Спальня (пом. 2)

Спальня (пом. 2) · вид изнутри помещения · размеры в мм, отметки в м

ПРЕДВАРИТЕЛЬНО · не для производства работ · открыто пунктов: 10 (реестр — л. 6, 7)

Развёртка стены В


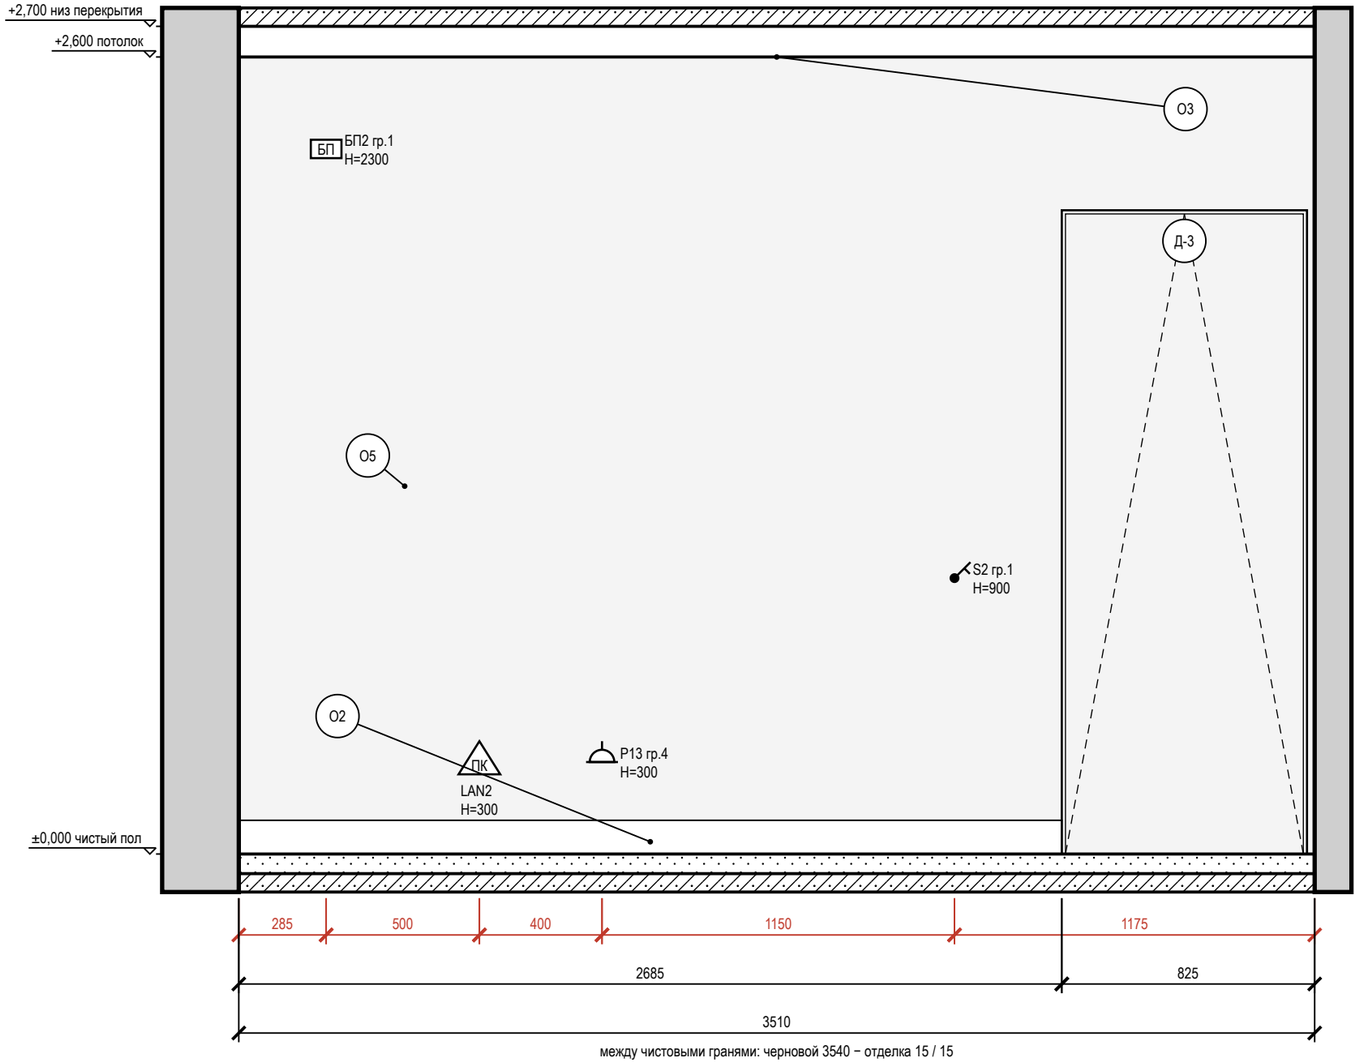


Схема развёрток (М 1:100)

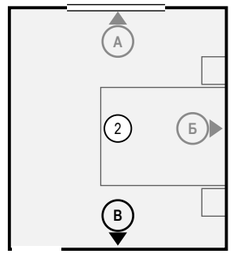

Условные обозначения

- розетка с заземляющим контактом; у знака — марка, ×N постов в рамке, гр. — группа щита, Н — высота оси, мм
- выключатель одноклавишный
- БП — блок питания LED, с доступом (люк от 100×100 мм)
- ПК — розетка компьютерная RJ45
- привязки точек и выводов от угла и от пола, мм
- мебель и приборы — фасад по расстановке (условно)
- дверь скрытого монтажа: полотно в плоскости стены (узел — на листе узлов)
- стены и перекрытия в сечении
- О1 — марка отделки по реестру отделки альбома
- А — марка развёртки: буква стены, стрелка — взгляд

Ведомость отделки (на листе)

Марка	Поверхность	Материал, изделие	Цвет, код	Кол.
О2	плинтус	плинтус МДФ, Orac Decor Luxxus, h 110 мм, SX184, шелковисто-матовая	NCS S 0300-N	2,7 м
О3	потолок	окраска, Tikkurila, глубокоматовая	NCS S 0300-N	13,9 м²
О5	стены	окраска, Tikkurila, глубокоматовая, подготовка Q3	NCS S 1502-Y50R	7,4 м²

Допущения и предложения на листе

Основа листа: размеры сняты с плана заказчика, контрольный обмер не выполнен (К-5); высота потолка 2700 мм принята: на плане заказчика не указана (К-5); подрайон климата не задан — принят не северный (жилые от 2,5 м) (К-4); толщины стен приняты: наружные 250 мм, перегородки 120 мм — не обмерены (К-5); разрешённая мощность 15 кВт принята по типовой квартире, технических условий нет (К-6).

См. лист открытых вопросов (лист 6, записи К-4–К-6).

Примечания

1. Развёртки — вид на стену изнутри помещения, по часовой стрелке; расположение — на схеме листа и на листе 60; размеры — в мм по чистовым поверхностям; отметки — в м от ±0,000; высоты Н — от чистого пола помещения до оси изделия, у декора — до центра.
2. Красная цепочка — привязки электроточек и выводов по осям от угла чистовых стен; высота Н — у знака, от чистого пола до оси; высоты мебели, проёмов и границ отделки — колонкой отметок слева. Стена с 5 и более точками или с мелкими звеньями привязок показана двумя видами: архитектурная развёртка (мебель, отделка, проёмы, высоты) и вид «Привязки» на отдельном листе — точки и выводы с марками, одна цепочка по осям и таблица привязок (каждая точка — строка).
3. У знака электроточки: марка (Р — розетка, S — выключатель, Св — светильник, ЭВ — вывод кабеля), ×N — число постов в рамке, гр. — группа щита, Н — высота оси от чистого пола, мм; группы по клавишам выключателя — на листе выключателей.
4. Схема мебели, приборов и декора не является технической документацией для производства мебели; габариты — по паспортам изделий.
5. Двери скрытого монтажа — полотно в плоскости стены, отделка стены по полотну, плинтус прерывается у короба (узел — на листе узлов).
6. Потолок — у каждой стены свой, по плану потолков (ПТ2); ступени — зоной, кромка короба перед нишей — тонкой линией; в поле потолка: ПТ1 +2,550.

1000 мм · печать 1:1

Изм.	Кол.уч	Лист	№ док.	Подп.	Дата
Разраб.		Кырлан А.С.			04.11.26
Пров.					
ГИП					
Н. контр.					
Утв.					

ГД-2026-006-АИ

Квартира 58 м²

Общая площадь 55,23* м² · * размеры приняты, не замерены (реестр — л. 6, 7, К-5)

Дизайн-проект интерьера

Стадия	Лист	Листов
РП	69	87

Развёртка стены В. Спальня (пом. 2)

М 1:20

Кырлан Александр Сергеевич


выпуск 04.11.2026 № 94e55e632e · стр. 77 из 96

Развёртки стен А, Б, В. Ванная (пом. 3)

Ванная (пом. 3) · вид изнутри помещения · размеры в мм, отметки в м


ПРЕДВАРИТЕЛЬНО · не для производства работ · открыто пунктов: 10 (реестр — л. 6, 7)

Развёртка стены А

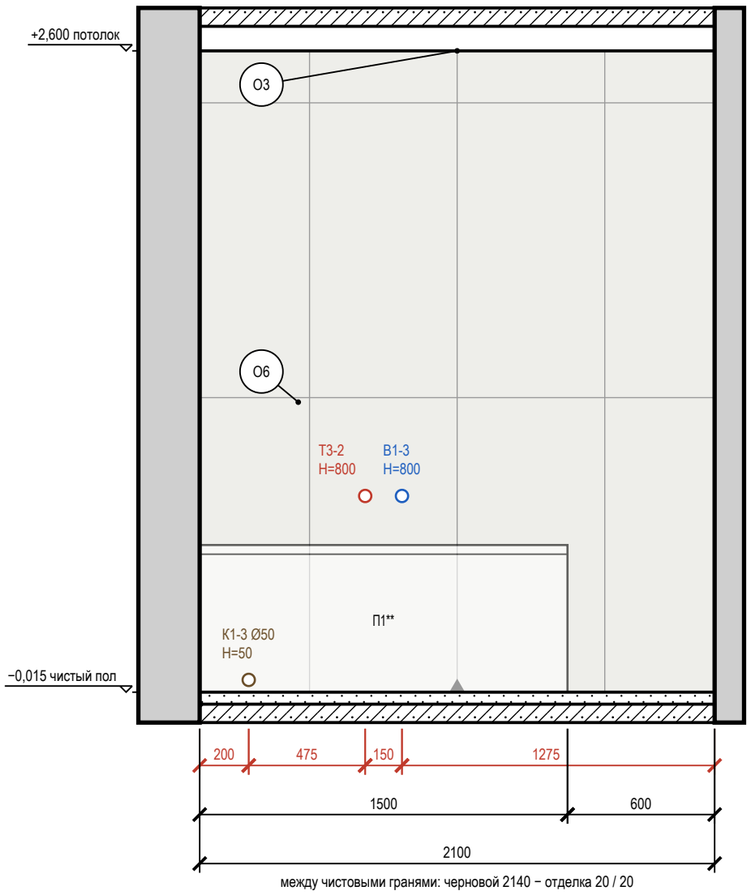


между чистовыми гранями: черновой 2140 − отделка 20 / 20

Развёртка стены Б

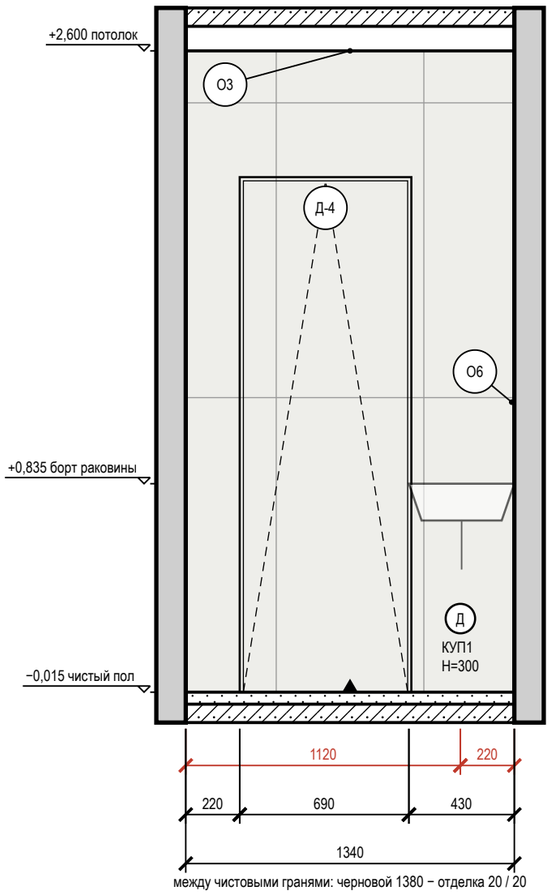


между чистовыми гранями: черновой 1380 − отделка 20 / 20

Развёртка стены В

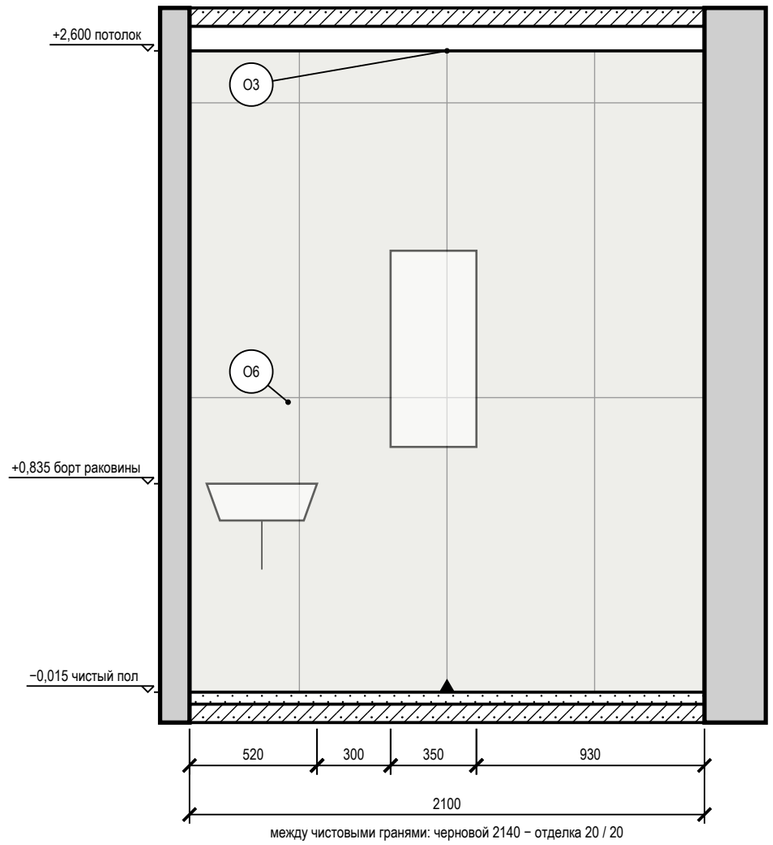

между чистовыми гранями: черновой 2140 − отделка 20 / 20

Схема развёрток (М 1:100)

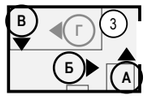

Условные обозначения

- вывод В1 (код — в ведомости привязок)
- вывод Т3 (код — в ведомости привязок)
- вывод К1 (код — в ведомости привязок)
- привязки точек и выводов от угла и от пола, мм
- мебель и приборы — фасад по расстановке (условно)
- дверь скрытого монтажа: полотно в плоскости стены (узел — на листе узлов)
- стены и перекрытия в сечении
- плитка: сетка швов по формату, ▲ — ось старта
- О1 — марка отделки по реестру отделки альбома
- А — марка развёртки: буква стены, стрелка — взгляд

Допущения и предложения на листе. Знак «**» предложено (согласовать). См. лист открытых вопросов (листы 6, 7).

Ведомость отделки (на листе)

Марка	Поверхность	Материал, изделие	Цвет, код	Кол.
О3	потолок	окраска, Tikkurila, глубокоматовая	NCS S 0300-N	3 м²
О6	стены	облицовка плиткой, Italon Charme Extra, 600×1200 мм, 610015000370	Italon 610015000370 «Charme Extra»	13 м²

Примечания

1. Развёртки — вид на стену изнутри помещения, по часовой стрелке; расположение — на схеме листа и на листе 60; размеры — в мм по чистовым поверхностям; отметки — в м от ±0,000; высоты Н — от чистого пола помещения до оси изделия, у декора — до центра.
2. Красная цепочка — привязки электроточек и выводов по осям от угла чистовых стен; высота Н — у знака, от чистого пола до оси; высоты мебели, проёмов и границ отделки — колонкой отметок слева. Стена с 5 и более точками или с мелкими звеньями привязок показана двумя видами: архитектурная развёртка (мебель, отделка, проёмы, высоты) и вид «Привязки» на отдельном листе — точки и выводы с марками, одна цепочка по осям и таблица привязок (каждая точка — строка).
3. Стена В показана двумя видами: здесь — архитектурная развёртка (мебель, отделка, проёмы, высоты), электроточки и выводы ВК с привязками и таблицей — на листе 71 («Привязки»).
4. У знака электроточки: марка (Р — розетка, S — выключатель, Св — светильник, ЭВ — вывод кабеля), ×N — число постов в рамке, гр. — группа щита, Н — высота оси от чистого пола, мм; группы по клавишам выключателя — на листе выключателей.
5. Схема мебели, приборов и декора не является технической документацией для производства мебели; габариты — по паспортам изделий.
6. Облицовка — по сетке швов, раскладка от оси стены (треугольник у пола); подрезки — по листу раскладки плитки.
7. Гидроизоляция в 2 слоя, заход на стены 200 мм; над ванной — до 2000 и 300 мм за борт — до облицовки, с актом скрытых работ и тестом проливом (узел — на листе узлов).
8. Двери скрытого монтажа — полотно в плоскости стены, отделка стены по полотну, плинтус прерывается у короба (узел — на листе узлов).

1000 мм · печать 1:1

Изм.	Кол.уч	Лист	№ док.	Подп.	Дата
Разраб.		Кырлан А.С.			04.11.26
Пров.					
ГИП					
Н. контр.					
Утв.					

ГД-2026-006-АИ

Квартира 58 м²

Общая площадь 55,23* м² · * размеры приняты, не замерены (реестр — л. 6, 7, К-5)

Дизайн-проект интерьера

Стадия	Лист	Листов
РП	70	87

Развёртки стен А, Б, В. Ванная (пом. 3)

М 1:25

Кырлан Александр Сергеевич

выпуск 04.11.2026 № 94e55e632e · стр. 78 из 96

Привязки электроточек и выводов ВК, стена В. Ванная (пом. 3)

Ванная (пом. 3) · вид изнутри помещения · привязки в мм, отметки в м · к развёртке на листе 70

ПРЕДВАРИТЕЛЬНО · не для производства работ · открыто пунктов: 10 (реестр — л. 6, 7)

Развёртка стены В: электроточки и выводы

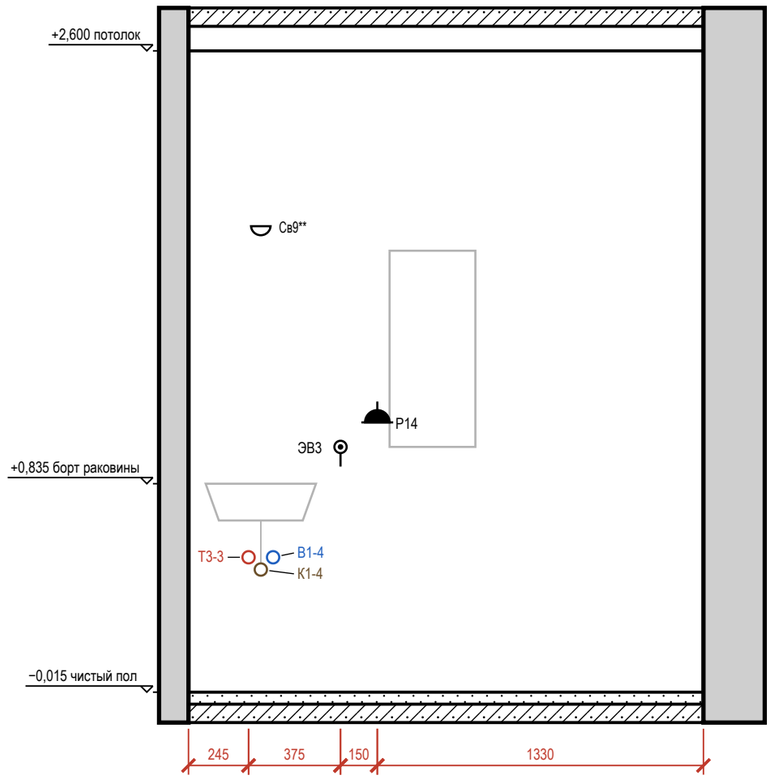



Таблица привязок электроточек и выводов

Марка	Назначение	От угла, мм	Н от пола, мм	Примечание
Т3-3	горячая вода — умывальник	245	550	межос. 100
К1-4	канализация — умывальник	295	500	Ø50
Св9**	светильник настенный	295	1900	гр. 1
В1-4	холодная вода — умывальник	345	550	межос. 100
ЭВ3	вывод кабеля: полотенцесушитель	620	1000	гр. 5
Р14	розетка: фен	770	1100	гр. 5, IP44

Условные обозначения

- розетка влагозащищённая IP44
- вывод кабеля для подключения прибора (без розетки), марка ЭВ
- светильник настенный (бра), Н — высота оси
- вывод В1 (код — в ведомости привязок)
- вывод Т3 (код — в ведомости привязок)
- вывод К1 (код — в ведомости привязок)
- привязки точек и выводов от угла и от пола, мм
- марка развёртки: буква стены, стрелка — взгляд

Схема развёрток (М 1:50)

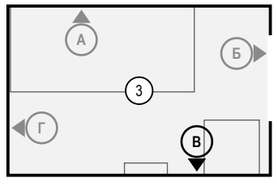

Примечания

1. Вид «Привязки» стены В — электроточки и выводы ВК; архитектурная развёртка (мебель, отделка, проёмы, высоты) — на листе 70, расположение — на листе 60. Мебель и приборы — подложкой для ориентира; их марки и обозначения мебели, проёмов и стен — там же.
2. Привязки — в мм: по горизонтали от левого чистового угла стены до оси изделия, Н — от чистого пола до оси; все точки — в таблице привязок. Красная цепочка — привязки по осям; точки ближе 150 мм одна к другой в цепочку не дробятся — их привязки только в таблице.
3. У знака — марка электроточки (Р — розетка, S — выключатель, Св — светильник, ЭВ — вывод кабеля); посты в рамке и группа щита — в графе «Примечание»; группы по клавишам выключателя — на листе выключателей.
4. Коды выводов ВК: В1 — холодная вода, Т3 — горячая вода, К1 — канализация; номер после дефиса — номер вывода на листе выводов сантехники.

Допущения и предложения на листе

Основа листа: размеры сняты с плана заказчика, контрольный обмер не выполнен (К-5); высота потолка 2700 мм принята: на плане заказчика не указана (К-5); подрайон климата не задан — принят не северный (жилые от 2,5 м) (К-4); толщины стен приняты: наружные 250 мм, перегородки 120 мм — не обмерены (К-5); разрешённая мощность 15 кВт принята по типовой квартире, технических условий нет (К-6).

Знак «**» — предложение проектировщика, заказчиком не утверждено (согласовать с заказчиком): Св9 — свет у зеркала — над зеркалом у умывальника по его оси (свет на лицо, а не над сантехникой).

См. лист открытых вопросов (лист 6, записи К-4–К-6).

1000 мм · печать 1:1

Изм.	Кол.уч	Лист	№ док.	Подп.	Дата
Разраб.		Кырлан А.С.			04.11.26
Пров.					
ГИП					
Н. контр.					
Утв.					

ГД-2026-006-АИ

Квартира 58 м²

Общая площадь 55,23* м² · * размеры приняты, не замерены (реестр — л. 6, 7, К-5)

Дизайн-проект интерьера

Стадия	Лист	Листов
РП	71	87

Привязки электроточек и выводов ВК, стена В. Ванная (пом. 3)

М 1:25

Кырлан Александр Сергеевич


выпуск 04.11.2026 № 94e55e632e · стр. 79 из 96

Развёртка стены Г. Ванная (пом. 3)

Ванная (пом. 3) · вид изнутри помещения · размеры в мм, отметки в м


ПРЕДВАРИТЕЛЬНО · не для производства работ · открыто пунктов: 10 (реестр — л. 6, 7)

Развёртка стены Г

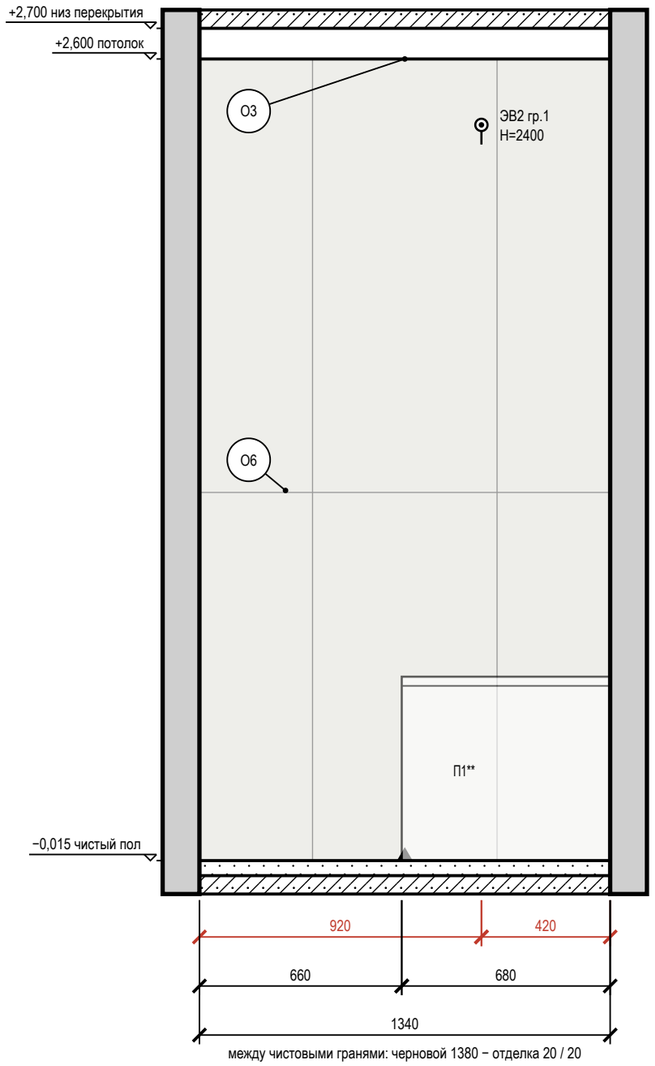

между чистовыми гранями: черновой 1380 − отделка 20 / 20

Схема развёрток (М 1:100)

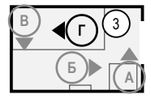

Условные обозначения

- вывод кабеля для подключения прибора (без розетки), марка ЭВ
- привязки точек и выводов от угла и от пола, мм
- мебель и приборы — фасад по расстановке (условно)
- стены и перекрытия в сечении
- плитка: сетка швов по формату, ▲ — ось старта
- О1 — марка отделки по реестру отделки альбома
- А — марка развёртки: буква стены, стрелка — взгляд

Ведомость отделки (на листе)

Марка	Поверхность	Материал, изделие	Цвет, код	Кол.
О3	потолок	окраска, Tikkurila, глубокоматовая	NCS S 0300-N	3 м²
О6	стены	облицовка плиткой, Italon Charme Extra, 600×1200 мм, 610015000370	Italon 610015000370 «Charme Extra»	3,5 м²

Допущения и предложения на листе

Основа листа: размеры сняты с плана заказчика, контрольный обмер не выполнен (К-5); высота потолка 2700 мм принята: на плане заказчика не указана (К-5); подрайон климата не задан — принят не северный (жилые от 2,5 м) (К-4); толщины стен приняты: наружные 250 мм, перегородки 120 мм — не обмерены (К-5); разрешённая мощность 15 кВт принята по типовой квартире, технических условий нет (К-6).

Знак «**» — предложение проектировщика, заказчиком не утверждено (согласовать с заказчиком): К-2: П1 — ванна 1500 вместо 1600 — не заходит в проход перед проёмом Д-4; перед ванной 680 мм — глубина помещения.

См. лист открытых вопросов (лист 6, записи К-2, К-4–К-6).

Примечания

1. Развёртки — вид на стену изнутри помещения, по часовой стрелке; расположение — на схеме листа и на листе 60; размеры — в мм по чистовым поверхностям; отметки — в м от ±0,000; высоты H — от чистого пола помещения до оси изделия, у декора — до центра.
2. Красная цепочка — привязки электроточек и выводов по осям от угла чистовых стен; высота H — у знака, от чистого пола до оси; высоты мебели, проёмов и границ отделки — колонкой отметок слева. Стена с 5 и более точками или с мелкими звеньями привязок показана двумя видами: архитектурная развёртка (мебель, отделка, проёмы, высоты) и вид «Привязки» на отдельном листе — точки и выводы с марками, одна цепочка по осям и таблица привязок (каждая точка — строка).
3. У знака электроточки: марка (Р — розетка, S — выключатель, Св — светильник, ЭВ — вывод кабеля), ×N — число постов в рамке, гр. — группа щита, H — высота оси от чистого пола, мм; группы по клавишам выключателя — на листе выключателей.
4. Схема мебели, приборов и декора не является технической документацией для производства мебели; габариты — по паспортам изделий.
5. Облицовка — по сетке швов, раскладка от оси стены (треугольник у пола); подрезки — по листу раскладки плитки.
6. Гидроизоляция в 2 слоя, заход на стены 200 мм; над ванной — до 2000 и 300 мм за борт — до облицовки, с актом скрытых работ и тестом проливом (узел — на листе узлов).

1000 мм · печать 1:1

Изм.	Кол.уч	Лист	№ док.	Подп.	Дата
Разраб.		Кырлан А.С.			04.11.26
Пров.					
ГИП					
Н. контр.					
Утв.					

ГД-2026-006-АИ

Квартира 58 м²

Общая площадь 55,23* м² · * размеры приняты, не замерены (реестр — л. 6, 7, К-5)

Дизайн-проект интерьера

Стадия	Лист	Листов
РП	72	87

Развёртка стены Г. Ванная (пом. 3)

М 1:20

Кырлан Александр Сергеевич


выпуск 04.11.2026 № 94e55e632e · стр. 80 из 96

Развёртки стен А, Б, В. Санузел (пом. 4)

Санузел (пом. 4) · вид изнутри помещения · размеры в мм, отметки в м


ПРЕДВАРИТЕЛЬНО · не для производства работ · открыто пунктов: 10 (реестр — л. 6, 7)

Развёртка стены А

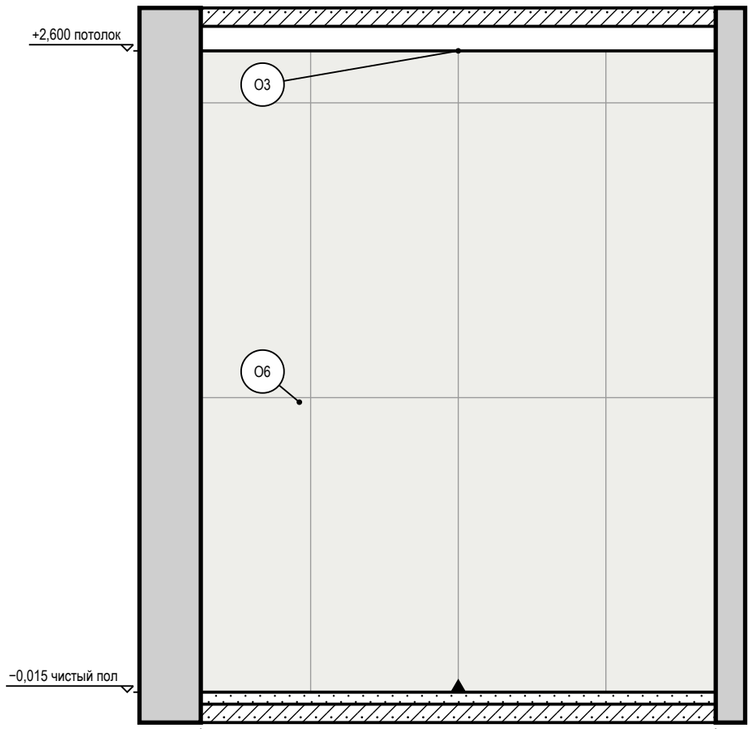


между чистовыми гранями: черновой 2140 − отделка 20 / 20

Развёртка стены Б

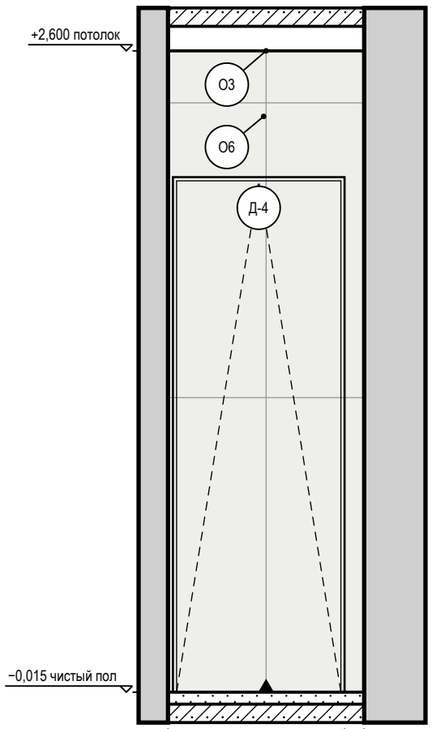


между чистовыми гранями: черновой 840 − отделка 20 / 20

Развёртка стены В

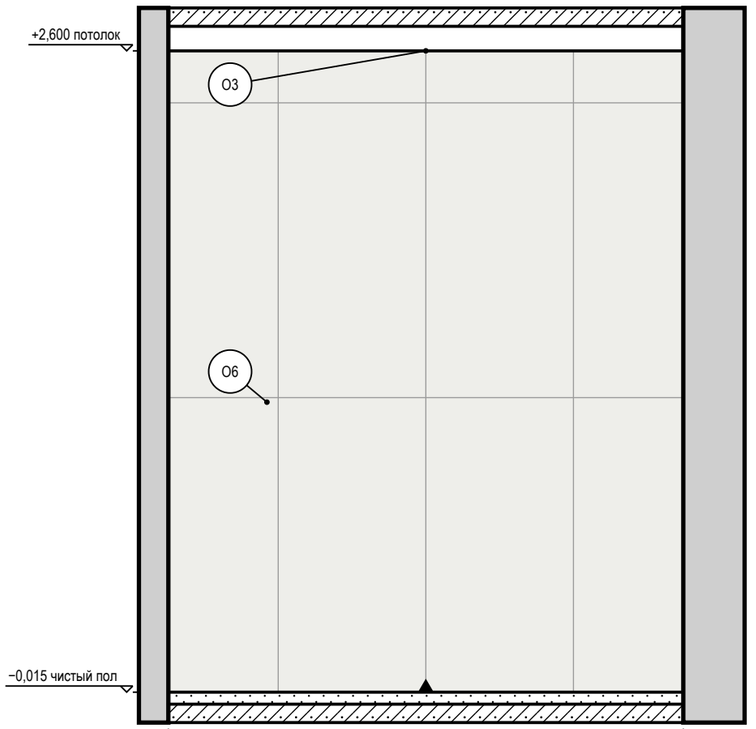

между чистовыми гранями: черновой 2140 − отделка 20 / 20

Схема развёрток (М 1:100)

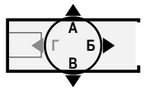

Условные обозначения

- мебель и приборы — фасад по расстановке (условно)
- дверь скрытого монтажа: полотно в плоскости стены (узел — на листе узлов)
- стены и перекрытия в сечении
- плитка: сетка швов по формату, ▲ — ось старта
- О1 — марка отделки по реестру отделки альбома
- А — марка развёртки: буква стены, стрелка — взгляд

Ведомость отделки (на листе)

Марка	Поверхность	Материал, изделие	Цвет, код	Кол.
О3	потолок	окраска, Tikkurila, глубокоматовая	NCS S 0300-N	1,8 м²
О6	стены	облицовка плиткой, Italon Charme Extra, 600×1200 мм, 610015000370	Italon 610015000370 «Charme Extra»	11,6 м²

Примечания

1. Развёртки — вид на стену изнутри помещения, по часовой стрелке; расположение — на схеме листа и на листе 60; размеры — в мм по чистовым поверхностям; отметки — в м от ±0,000; высоты Н — от чистого пола помещения до оси изделия, у декора — до центра.
2. Схема мебели, приборов и декора не является технической документацией для производства мебели; габариты — по паспортам изделий.
3. Облицовка — по сетке швов, раскладка от оси стены (треугольник у пола); подрезки — по листу раскладки плитки.
4. Гидроизоляция в 2 слоя, заход на стены 200 мм — до облицовки, с актом скрытых работ и тестом проливом (узел — на листе узлов).
5. Двери скрытого монтажа — полотно в плоскости стены, отделка стены по полотну, плинтус прерывается у короба (узел — на листе узлов).

Допущения и предложения на листе

Основа листа: размеры сняты с плана заказчика, контрольный обмер не выполнен (К-5); высота потолка 2700 мм принята: на плане заказчика не указана (К-5); подрайон климата не задан — принят не северный (жилые от 2,5 м) (К-4); толщины стен приняты: наружные 250 мм, перегородки 120 мм — не обмерены (К-5); разрешённая мощность 15 кВт принята по типовой квартире, технических условий нет (К-6).

См. лист открытых вопросов (лист 6, записи К-4–К-6).

1000 мм · печать 1:1

Изм.	Кол.уч	Лист	№ док.	Подп.	Дата
Разраб.		Кырлан А.С.			04.11.26
Пров.					
ГИП					
Н. контр.					
Утв.					

ГД-2026-006-АИ

Квартира 58 м²

Общая площадь 55,23* м² · * размеры приняты, не замерены (реестр — л. 6, 7, К-5)

Дизайн-проект интерьера

Стадия	Лист	Листов
РП	73	87

Развёртки стен А, Б, В. Санузел (пом. 4)

М 1:25

Кырлан Александр Сергеевич


выпуск 04.11.2026 № 94e55e632e · стр. 81 из 96

Развёртка стены Г. Санузел (пом. 4)

Санузел (пом. 4) · вид изнутри помещения · размеры в мм, отметки в м


ПРЕДВАРИТЕЛЬНО · не для производства работ · открыто пунктов: 10 (реестр — л. 6, 7)

Развёртка стены Г

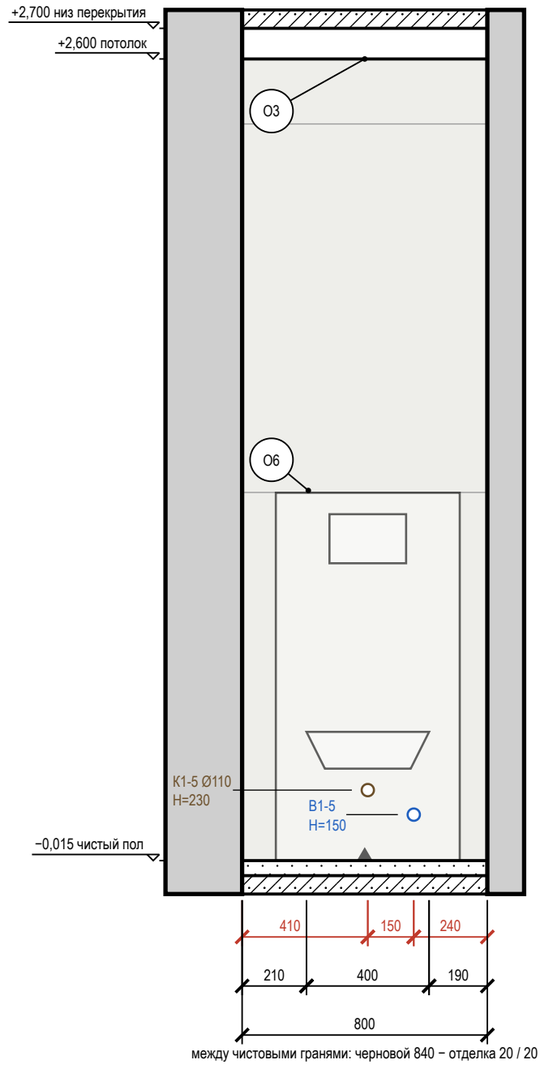

между чистовыми гранями: черновой 840 − отделка 20 / 20

Схема развёрток (М 1:100)

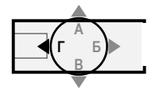

Условные обозначения

- вывод В1 (код — в ведомости привязок)
- вывод К1 (код — в ведомости привязок)
- привязки точек и выводов от угла и от пола, мм
- мебель и приборы — фасад по расстановке (условно)
- стены и перекрытия в сечении
- плитка: сетка швов по формату, ▲ — ось старта
- О1 — марка отделки по реестру отделки альбома
- А — марка развёртки: буква стены, стрелка — взгляд

Ведомость отделки (на листе)

Марка	Поверхность	Материал, изделие	Цвет, код	Кол.
О3	потолок	окраска, Tikkurila, глубокоматовая	NCS S 0300-N	1,8 м²
О6	стены	облицовка плиткой, Italon Charme Extra, 600×1200 мм, 610015000370	Italon 610015000370 «Charme Extra»	2,1 м²

Допущения и предложения на листе

Основа листа: размеры сняты с плана заказчика, контрольный обмер не выполнен (К-5); высота потолка 2700 мм принята: на плане заказчика не указана (К-5); подрайон климата не задан — принят не северный (жилые от 2,5 м) (К-4); толщины стен приняты: наружные 250 мм, перегородки 120 мм — не обмерены (К-5); разрешённая мощность 15 кВт принята по типовой квартире, технических условий нет (К-6).

См. лист открытых вопросов (лист 6, записи К-4–К-6).

Примечания

1. Развёртки — вид на стену изнутри помещения, по часовой стрелке; расположение — на схеме листа и на листе 60; размеры — в мм по чистовым поверхностям; отметки — в м от ±0,000; высоты Н — от чистого пола помещения до оси изделия, у декора — до центра.
2. Красная цепочка — привязки электроточек и выводов по осям от угла чистовых стен; высота Н — у знака, от чистого пола до оси; высоты мебели, проёмов и границ отделки — колонкой отметок слева. Стена с 5 и более точками или с мелкими звеньями привязок показана двумя видами: архитектурная развёртка (мебель, отделка, проёмы, высоты) и вид «Привязки» на отдельном листе — точки и выводы с марками, одна цепочка по осям и таблица привязок (каждая точка — строка).
3. У знака электроточки: марка (Р — розетка, S — выключатель, Св — светильник, ЭВ — вывод кабеля), ×N — число постов в рамке, гр. — группа щита, Н — высота оси от чистого пола, мм; группы по клавишам выключателя — на листе выключателей.
4. Схема мебели, приборов и декора не является технической документацией для производства мебели; габариты — по паспортам изделий (* — высота не задана в проекте, показана по типовому изделию).
5. Облицовка — по сетке швов, раскладка от оси стены (треугольник у пола); подрезки — по листу раскладки плитки.
6. Гидроизоляция в 2 слоя, заход на стены 200 мм — до облицовки, с актом скрытых работ и тестом проливом (узел — на листе узлов).

1000 мм · печать 1:1

Изм.	Кол.уч	Лист	№ док.	Подп.	Дата
Разраб.		Кырлан А.С.			04.11.26
Пров.					
ГИП					
Н. контр.					
Утв.					

ГД-2026-006-АИ

Квартира 58 м²

Общая площадь 55,23* м² · * размеры приняты, не замерены (реестр — л. 6, 7, К-5)

Дизайн-проект интерьера

Стадия	Лист	Листов
РП	74	87

Развёртка стены Г. Санузел (пом. 4)

М 1:20

Кырлан Александр Сергеевич


выпуск 04.11.2026 № 94e55e632e · стр. 82 из 96

Развёртки стен А, Б. Прихожая (пом. 5)

Прихожая (пом. 5) · вид изнутри помещения · размеры в мм, отметки в м


ПРЕДВАРИТЕЛЬНО · не для производства работ · открыто пунктов: 10 (реестр — л. 6, 7)

Развёртка стены А

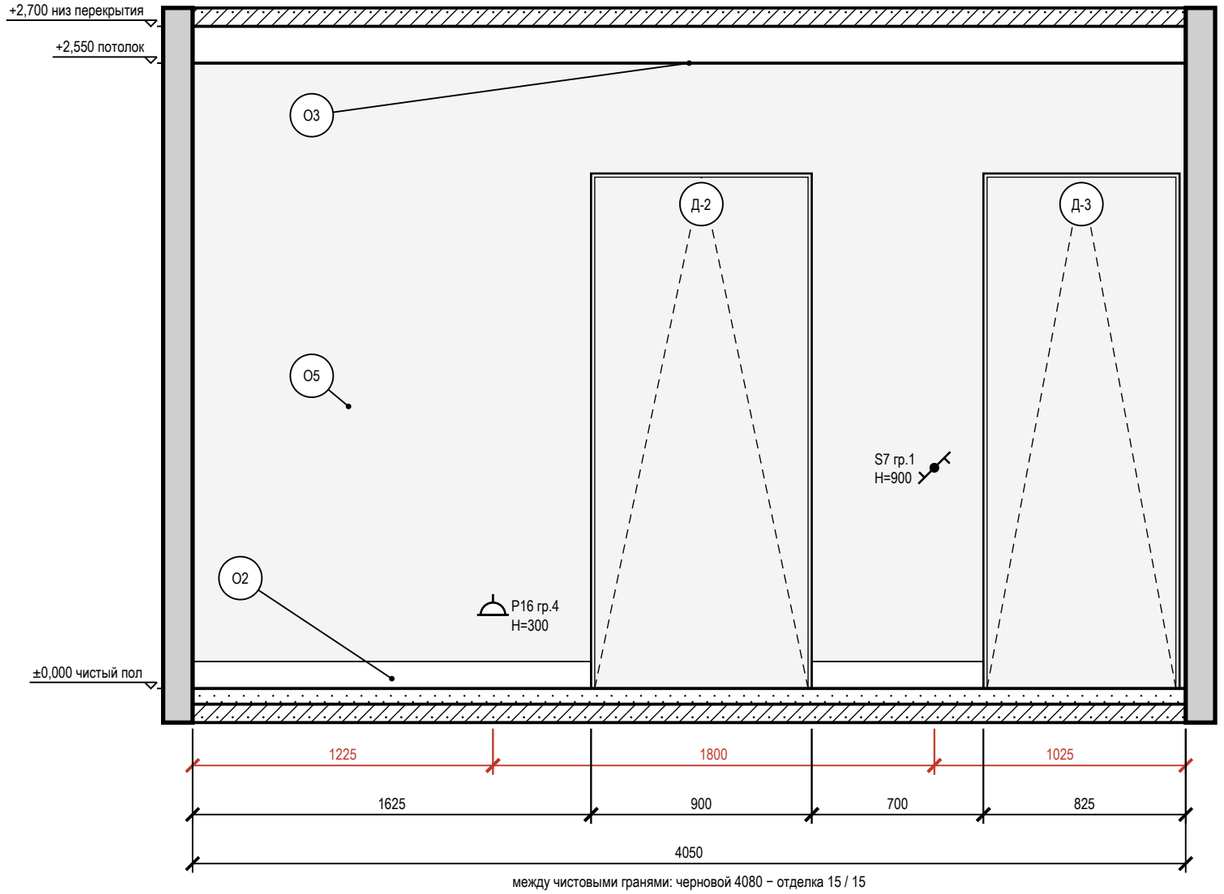


между чистовыми гранями: черновой 4080 − отделка 15 / 15

Развёртка стены Б

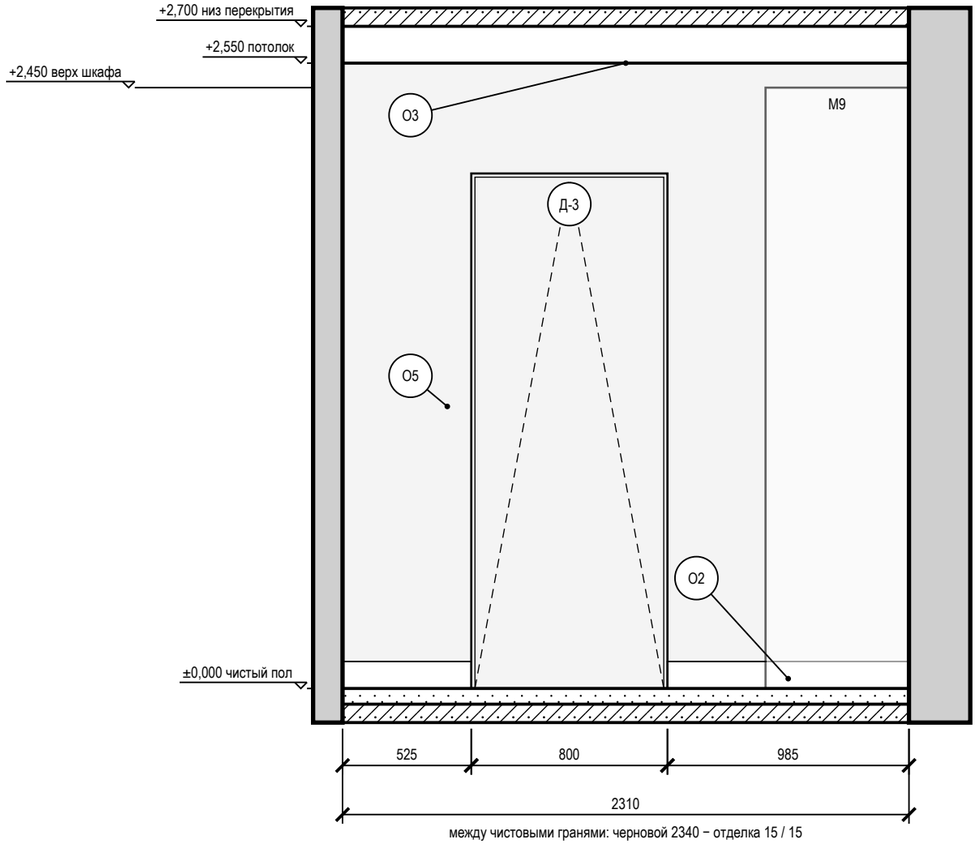

между чистовыми гранями: черновой 2340 − отделка 15 / 15

Схема развёрток (М 1:100)

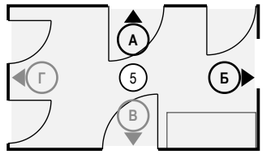

Условные обозначения

- розетка с заземляющим контактом; у знака — марка, ×N постов в рамке, гр. — группа щита, Н — высота оси, мм
- выключатель одноклавишный
- выключатель с проходной или перекрёстной клавишей (обратный флажок); тип клавиши — в подписи
- привязки точек и выводов от угла и от пола, мм
- мебель и приборы — фасад по расстановке (условно)
- дверь скрытого монтажа: полотно в плоскости стены (узел — на листе узлов)
- стены и перекрытия в сечении
- О1 — марка отделки по реестру отделки альбома
- А — марка развёртки: буква стены, стрелка — взгляд

Ведомость отделки (на листе)

Марка	Поверхность	Материал, изделие	Цвет, код	Кол.
О2	плинтус	плинтус МДФ, Orac Decor Luxxus, h 110 мм, SX184, шелковисто-матовая	NCS S 0300-N	3,8 м
О3	потолок	окраска, Tikkurila, глубокоматовая	NCS S 0300-N	9,6 м²
О5	стены	окраска, Tikkurila, шелковисто-матовая, подготовка Q3	NCS S 1502-Y50R	11 м²

Допущения и предложения на листе. Основа листа: размеры сняты с плана заказчика, контрольный обмер не выполнен (К-5); высота потолка 2700 мм принята: на плане заказчика не указана (К-5); подрайон климата не задан — принят не северный (жилые от 2,5 м) (К-4); толщины стен приняты: наружные 250 мм, перегородки 120 мм — не обмерены (К-5); разрешённая мощность 15 кВт принята по типовой квартире, технических условий нет (К-6). См. лист открытых вопросов (лист 6, записи К-4–К-6).

Примечания

1. Развёртки — вид на стену изнутри помещения, по часовой стрелке; расположение — на схеме листа и на листе 60; размеры — в мм по чистовым поверхностям; отметки — в м от ±0,000; высоты Н — от чистого пола помещения до оси изделия, у декора — до центра.
2. Красная цепочка — привязки электроточек и выводов по осям от угла чистовых стен; высота Н — у знака, от чистого пола до оси; высоты мебели, проёмов и границ отделки — колонкой отметок слева. Стена с 5 и более точками или с мелкими звеньями привязок показана двумя видами: архитектурная развёртка (мебель, отделка, проёмы, высоты) и вид «Привязки» на отдельном листе — точки и выводы с марками, одна цепочка по осям и таблица привязок (каждая точка — строка).
3. У знака электроточки: марка (Р — розетка, S — выключатель, Св — светильник, ЭВ — вывод кабеля), ×N — число постов в рамке, гр. — группа щита, Н — высота оси от чистого пола, мм; группы по клавишам выключателя — на листе выключателей.
4. Схема мебели, приборов и декора не является технической документацией для производства мебели; габариты — по паспортам изделий.
5. Двери скрытого монтажа — полотно в плоскости стены, отделка стены по полотну, плинтус прерывается у короба (узел — на листе узлов).
6. Потолок — у каждой стены свой, по плану потолков (ПТ1); ступени — зоной, кромка короба перед нишей — тонкой линией; в поле потолка: ПТ2 +2,600.

1000 мм · печать 1:1

Изм.	Кол.уч	Лист	№ док.	Подп.	Дата
Разраб.		Кырлан А.С.			04.11.26
Пров.					
ГИП					
Н. контр.					
Утв.					

ГД-2026-006-АИ

Квартира 58 м²

Общая площадь 55,23* м² · * размеры приняты, не замерены (реестр — л. 6, 7, К-5)

Дизайн-проект интерьера

Стадия	Лист	Листов
РП	75	87

Развёртки стен А, Б. Прихожая (пом. 5)

М 1:25

Кырлан Александр Сергеевич


выпуск 04.11.2026 № 94e55e632e · стр. 83 из 96

Развёртки стен В, Г. Прихожая (пом. 5)

Прихожая (пом. 5) · вид изнутри помещения · размеры в мм, отметки в м


ПРЕДВАРИТЕЛЬНО · не для производства работ · открыто пунктов: 10 (реестр — л. 6, 7)

Развёртка стены В

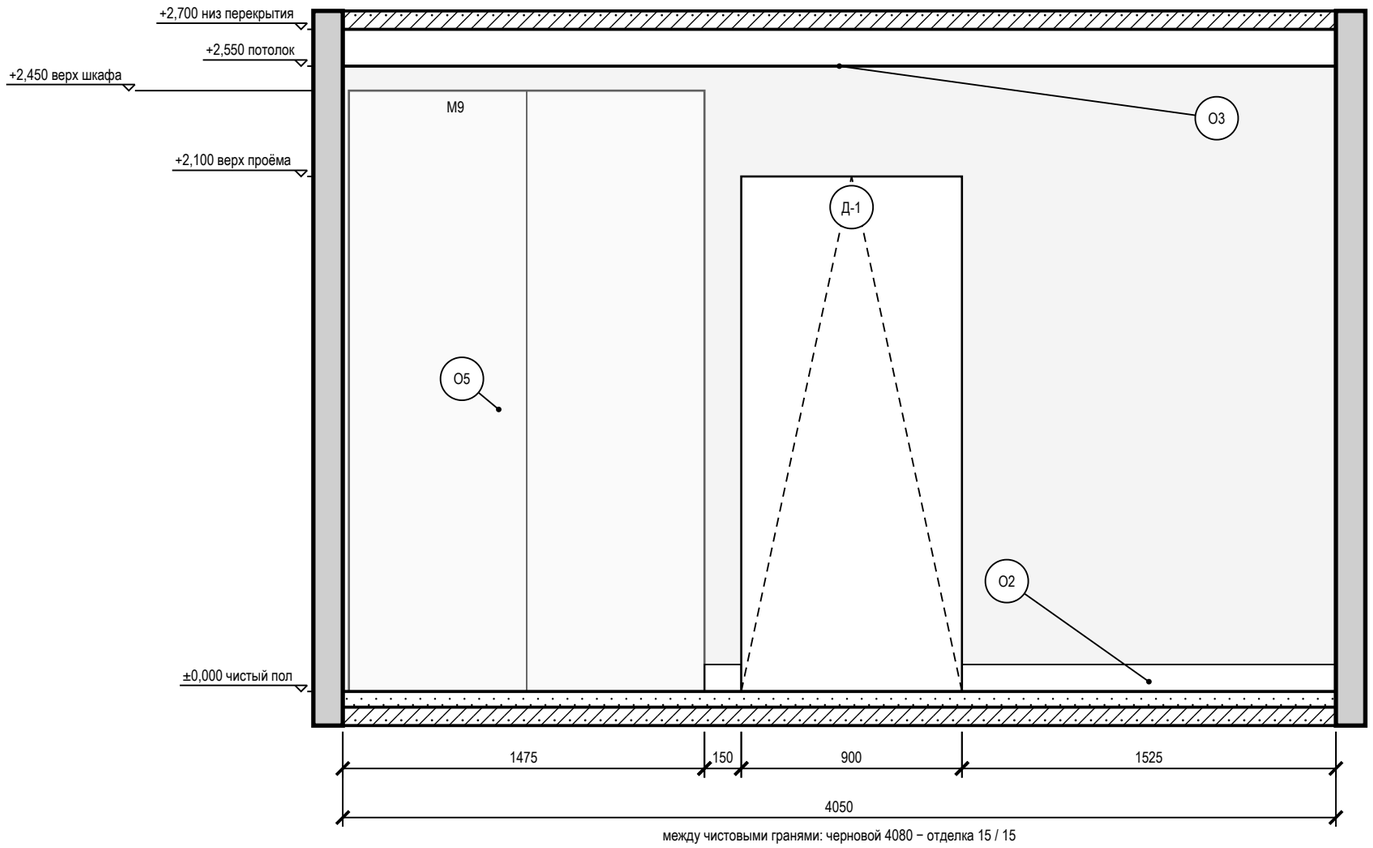


между чистовыми гранями: черновой 4080 − отделка 15 / 15

Развёртка стены Г

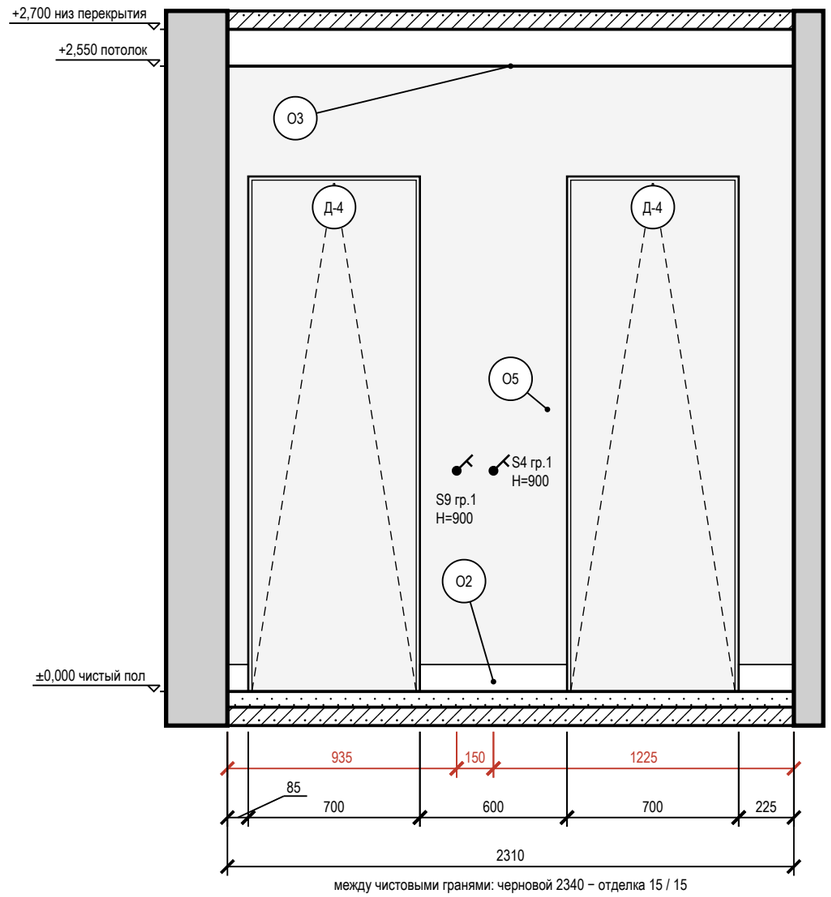

между чистовыми гранями: черновой 2340 − отделка 15 / 15

Схема развёрток (М 1:100)

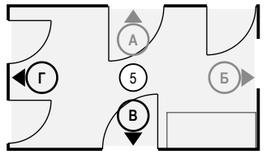

Условные обозначения

- выключатель одноклавишный
- привязки точек и выводов от угла и от пола, мм
- мебель и приборы — фасад по расстановке (условно)
- дверь скрытого монтажа: полотно в плоскости стены (узел — на листе узлов)
- дверной проём; марка двери — в кружке
- стены и перекрытия в сечении
- О1 — марка отделки по реестру отделки альбома
- А — марка развёртки: буква стены, стрелка — взгляд

Допущения и предложения на листе

Основа листа: размеры сняты с плана заказчика, контрольный обмер не выполнен (К-5); высота потолка 2700 мм принята: на плане заказчика не указана (К-5); подрайон климата не задан — принят не северный (жилые от 2,5 м) (К-4); толщины стен приняты: наружные 250 мм, перегородки 120 мм — не обмерены (К-5); разрешённая мощность 15 кВт принята по типовой квартире, технических условий нет (К-6).
См. лист открытых вопросов (лист 6, записи К-4–К-6).

Ведомость отделки (на листе)

Марка	Поверхность	Материал, изделие	Цвет, код	Кол.
О2	плинтус	плинтус МДФ, Orac Decor Luxxus, h 110 мм, SX184, шелковисто-матовая	NCS S 0300-N	2,6 м
О3	потолок	окраска, Tikkurila, глубокоматовая	NCS S 0300-N	9,6 м²
О5	стены	окраска, Tikkurila, шелковисто-матовая, подготовка Q3	NCS S 1502-Y50R	11,4 м²

Примечания

1. Развёртки — вид на стену изнутри помещения, по часовой стрелке; расположение — на схеме листа и на листе 60; размеры — в мм по чистовым поверхностям; отметки — в м от ±0,000; высоты Н — от чистого пола помещения до оси изделия, у декора — до центра.
2. Красная цепочка — привязки электроточек и выводов по осям от угла чистовых стен; высота Н — у знака, от чистого пола до оси; высоты мебели, проёмов и границ отделки — колонкой отметок слева. Стена с 5 и более точками или с мелкими звеньями привязок показана двумя видами: архитектурная развёртка (мебель, отделка, проёмы, высоты) и вид «Привязки» на отдельном листе — точки и выводы с марками, одна цепочка по осям и таблица привязок (каждая точка — строка).
3. Стена В показана двумя видами: здесь — архитектурная развёртка (мебель, отделка, проёмы, высоты), электроточки и выводы ВК с привязками и таблицей — на листе 77 («Привязки»).
4. У знака электроточки: марка (Р — розетка, S — выключатель, Св — светильник, ЭВ — вывод кабеля), ×N — число постов в рамке, гр. — группа щита, Н — высота оси от чистого пола, мм; группы по клавишам выключателя — на листе выключателей.
5. Схема мебели, приборов и декора не является технической документацией для производства мебели; габариты — по паспортам изделий.
6. Двери скрытого монтажа — полотно в плоскости стены, отделка стены по полотну, плинтус прерывается у короба (узел — на листе узлов).
7. Потолок — у каждой стены свой, по плану потолков (ПТ1); ступени — зоной, кромка короба перед нишей — тонкой линией; в поле потолка: ПТ2 +2,600.

1000 мм · печать 1:1

Изм.	Кол.уч	Лист	№ док.	Подп.	Дата
Разраб.		Кырлан А.С.			04.11.26
Пров.					
ГИП					
Н. контр.					
Утв.					

ГД-2026-006-АИ

Квартира 58 м²

Общая площадь 55,23* м² · * размеры приняты, не замерены (реестр — л. 6, 7, К-5)

Дизайн-проект интерьера

Стадия	Лист	Листов
РП	76	87

Развёртки стен В, Г. Прихожая (пом. 5)

М 1:25

Кырлан Александр Сергеевич

выпуск 04.11.2026 № 94e55e632e · стр. 84 из 96

Привязки электроточек, стена В. Прихожая (пом. 5)

Прихожая (пом. 5) · вид изнутри помещения · привязки в мм, отметки в м · к развёртке на листе 76

ПРЕДВАРИТЕЛЬНО · не для производства работ · открыто пунктов: 10 (реестр — л. 6, 7)

Развёртка стены В: электроточки и выводы

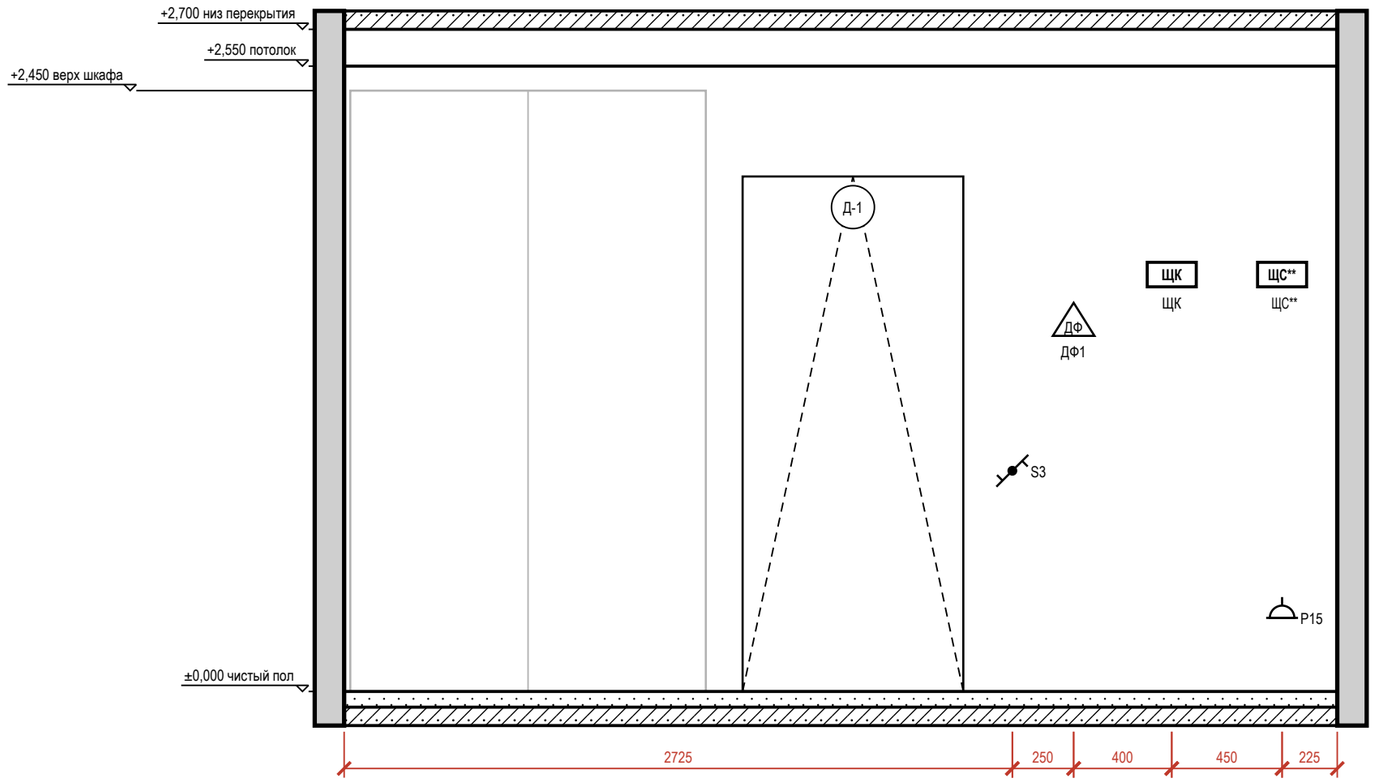



Таблица привязок электроточек и выводов

Марка	Назначение	От угла, мм	Н от пола, мм	Примечание
S3	выключатель	2725	900	гр. 1
ДФ1	домофон: трубка домофона	2975	1500	
ЩК	щит	3375	1700	
Р15	розетка: питание ЩС** (роутер, ИБП)	3825	300	гр. 4
ЩС**	щит: щит слаботочный: ввод провайдера, роутер	3825	1700	

Условные обозначения

- розетка с заземляющим контактом; у знака — марка, ×N постов в рамке, гр. — группа щита, Н — высота оси, мм
- выключатель одноклавишный
- выключатель с проходной или перекрёстной клавишей (обратный флажок); тип клавиши — в подписи
- ДФ — трубка или монитор домофона
- ЩК — щит квартирный
- привязки точек и выводов от угла и от пола, мм
- A — марка развёртки: буква стены, стрелка — взгляд

Схема развёрток (М 1:50)

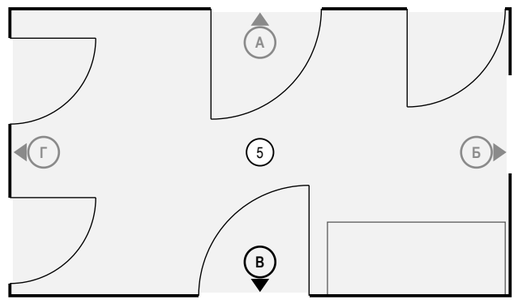

Примечания

1. Вид «Привязки» стены В — электроточки и выводы ВК; архитектурная развёртка (мебель, отделка, проёмы, высоты) — на листе 76, расположение — на листе 60. Мебель и приборы — подложкой для ориентира; их марки и обозначения мебели, проёмов и стен — там же.
2. Привязки — в мм: по горизонтали от левого чистового угла стены до оси изделия, Н — от чистого пола до оси; все точки — в таблице привязок. Красная цепочка — привязки по осям; точки ближе 150 мм одна к другой в цепочку не дробятся — их привязки только в таблице.
3. У знака — марка электроточки (Р — розетка, S — выключатель, Св — светильник, ЭВ — вывод кабеля); посты в рамке и группа щита — в графе «Примечание»; группы по клавишам выключателя — на листе выключателей.

Допущения и предложения на листе

Основа листа: размеры сняты с плана заказчика, контрольный обмер не выполнен (К-5); высота потолка 2700 мм принята: на плане заказчика не указана (К-5); подрайон климата не задан — принят не северный (жилые от 2,5 м) (К-4); толщины стен приняты: наружные 250 мм, перегородки 120 мм — не обмерены (К-5); разрешённая мощность 15 кВт принята по типовой квартире, технических условий нет (К-6).

Знак «**» — предложение проектировщика, заказчиком не утверждено (согласовать с заказчиком): ЩС — щит слаботочный: место и состав.

См. лист открытых вопросов (лист 6, записи К-4–К-6).

1000 мм · печать 1:1

Изм.	Кол.уч	Лист	№ док.	Подп.	Дата
Разраб.		Кырлан А.С.			04.11.26
Пров.					
ГИП					
Н. контр.					
Утв.					

ГД-2026-006-АИ

Квартира 58 м²

Общая площадь 55,23* м² · * размеры приняты, не замерены (реестр — л. 6, 7, К-5)

Дизайн-проект интерьера

Стадия	Лист	Листов
РП	77	87

Привязки электроточек, стена В. Прихожая (пом. 5)

М 1:25

Кырлан Александр Сергеевич


выпуск 04.11.2026 № 94e55e632e · стр. 85 из 96

Развёртки стен А, Б. Гардеробная (пом. 6)

Гардеробная (пом. 6) · вид изнутри помещения · размеры в мм, отметки в м


ПРЕДВАРИТЕЛЬНО · не для производства работ · открыто пунктов: 10 (реестр — л. 6, 7)

Развёртка стены А

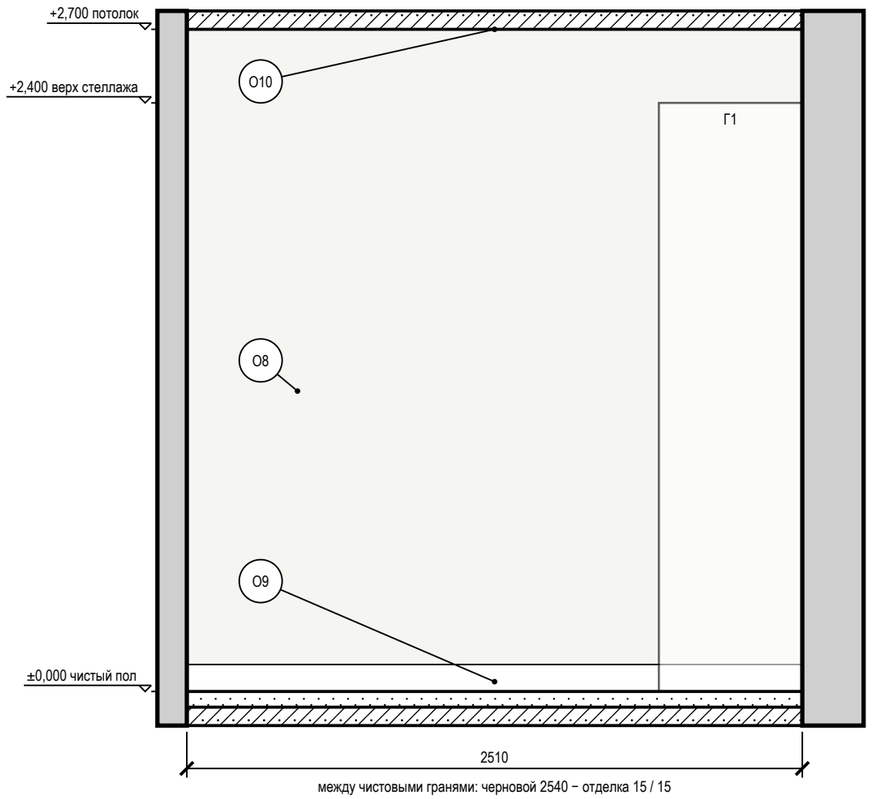

между чистовыми гранями: черновой 2540 − отделка 15 / 15

Развёртка стены Б

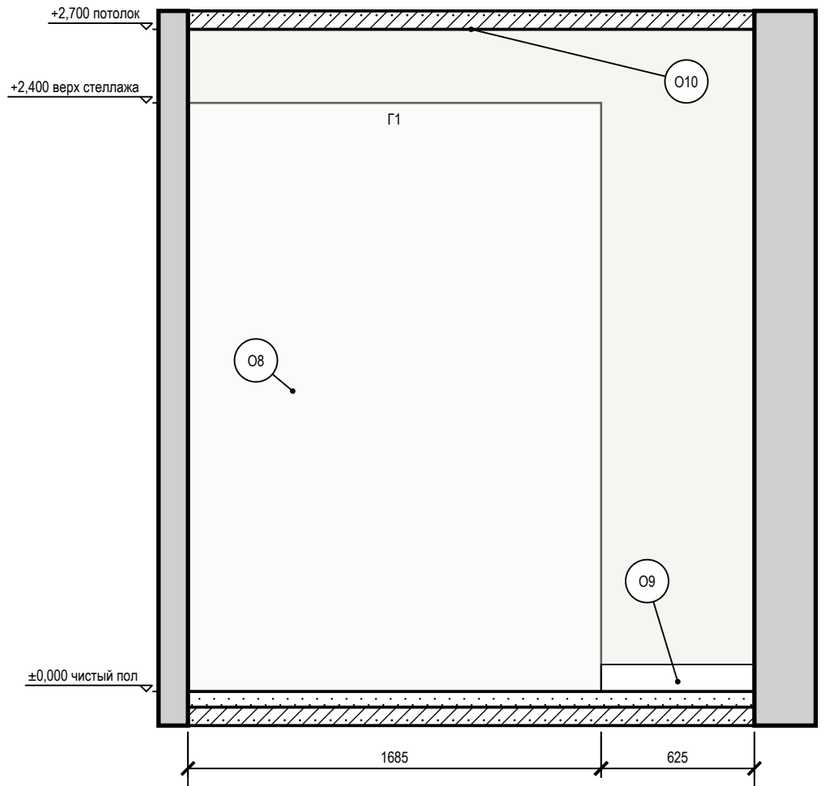


между чистовыми гранями: черновой 2340 − отделка 15 / 15

Условные обозначения

- мебель и приборы — фасад по расстановке (условно)
- стены и перекрытия в сечении
- окраска: тон — цвет по коду производителя (условно)
- О1 — марка отделки по реестру отделки альбома
- А — марка развёртки: буква стены, стрелка — взгляд

Схема развёрток (М 1:100)

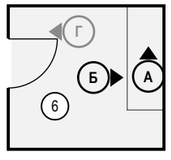

Ведомость отделки (на листе)

Марка	Поверхность	Материал, изделие	Цвет, код	Кол.
О8	стены	окраска, Tikkurila Harmony, матовая, подготовка Q3	Tikkurila V503 «Winter»	13 м²
О9	плинтус	плинтус МДФ, Orac Decor Luxxus, h 110 мм, SX184	Tikkurila V503 «Winter»	3,1 м
О10	потолок	окраска, Tikkurila Anti-Reflex 2, глубокоматовая, подготовка Q3	Tikkurila V503 «Winter»	5,9 м²

Примечания

1. Развёртки — вид на стену изнутри помещения, по часовой стрелке; расположение — на схеме листа и на листе 60; размеры — в мм по чистовым поверхностям; отметки — в м от ±0,000; высоты Н — от чистого пола помещения до оси изделия, у декора — до центра.
2. Схема мебели, приборов и декора не является технической документацией для производства мебели; габариты — по паспортам изделий.

Допущения и предложения на листе

Основа листа: размеры сняты с плана заказчика, контрольный обмер не выполнен (К-5); высота потолка 2700 мм принята: на плане заказчика не указана (К-5); подрайон климата не задан — принят не северный (жилые от 2,5 м) (К-4); толщины стен приняты: наружные 250 мм, перегородки 120 мм — не обмерены (К-5); разрешённая мощность 15 кВт принята по типовой квартире, технических условий нет (К-6).

См. лист открытых вопросов (лист 6, записи К-4–К-6).

1000 мм · печать 1:1

Изм.	Кол.уч	Лист	№ док.	Подп.	Дата
Разраб.		Кырлан А.С.			04.11.26
Пров.					
ГИП					
Н. контр.					
Утв.					

ГД-2026-006-АИ

Квартира 58 м²

Общая площадь 55,23* м² · * размеры приняты, не замерены (реестр — л. 6, 7, К-5)

Дизайн-проект интерьера

Стадия	Лист	Листов
РП	78	87

Развёртки стен А, Б. Гардеробная (пом. 6)

М 1:25

Кырлан Александр Сергеевич


выпуск 04.11.2026 № 94e55e632e · стр. 86 из 96

Развёртка стены Г. Гардеробная (пом. 6)

Гардеробная (пом. 6) · вид изнутри помещения · размеры в мм, отметки в м


ПРЕДВАРИТЕЛЬНО · не для производства работ · открыто пунктов: 10 (реестр — л. 6, 7)

Развёртка стены Г

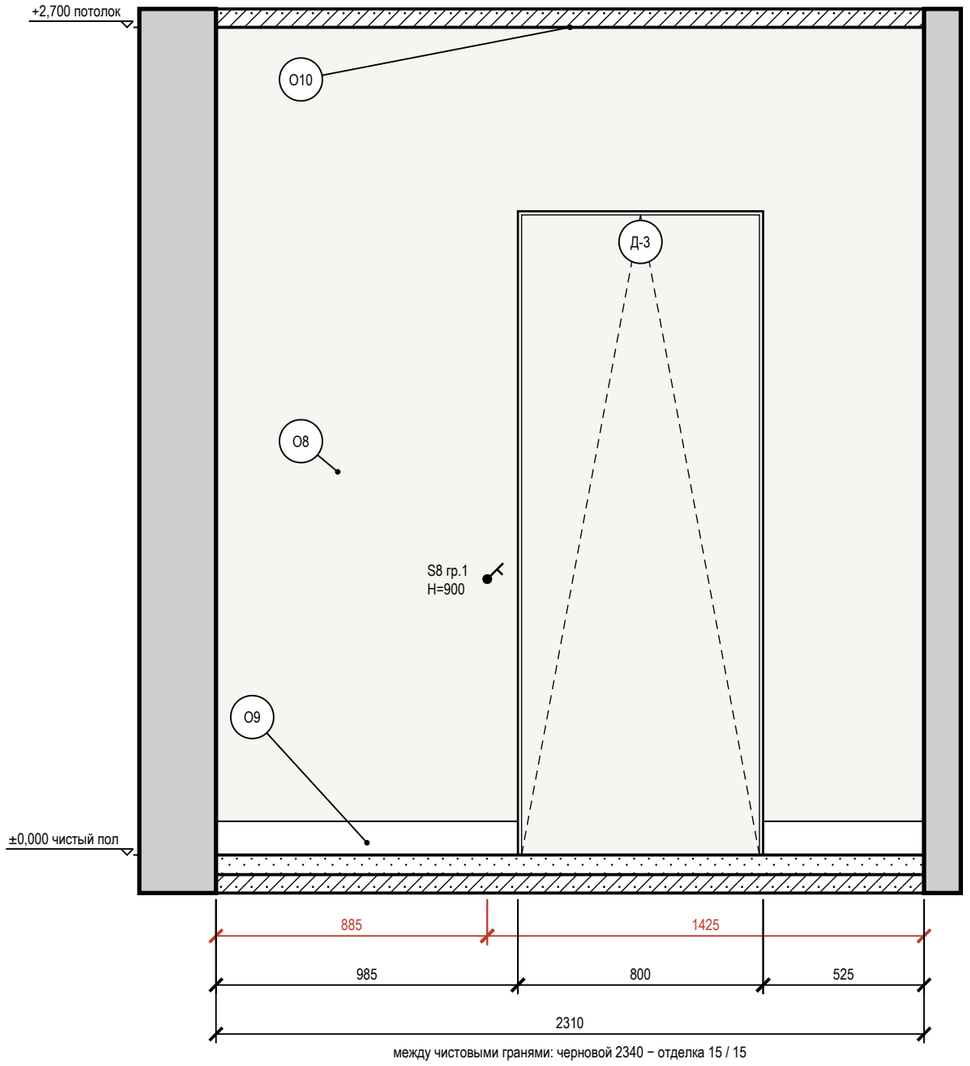

между чистовыми гранями: черновой 2340 − отделка 15 / 15

Схема развёрток (М 1:100)

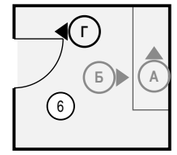

Условные обозначения

- выключатель одноклавишный
- привязки точек и выводов от угла и от пола, мм
- мебель и приборы — фасад по расстановке (условно)
- дверь скрытого монтажа: полотно в плоскости стены (узел — на листе узлов)
- стены и перекрытия в сечении
- окраска: тон — цвет по коду производителя (условно)
- О1 — марка отделки по реестру отделки альбома
- А — марка развёртки: буква стены, стрелка — взгляд

Ведомость отделки (на листе)

Марка	Поверхность	Материал, изделие	Цвет, код	Кол.
О8	стены	окраска, Tikkurila Harmony, матовая, подготовка Q3	Tikkurila V503 «Winter»	4,6 м²
О9	плинтус	плинтус МДФ, Orac Decor Luxxus, h 110 мм, SX184	Tikkurila V503 «Winter»	1,5 м
О10	потолок	окраска, Tikkurila Anti-Reflex 2, глубокоматовая, подготовка Q3	Tikkurila V503 «Winter»	5,9 м²

Допущения и предложения на листе

Основа листа: размеры сняты с плана заказчика, контрольный обмер не выполнен (К-5); высота потолка 2700 мм принята: на плане заказчика не указана (К-5); подрайон климата не задан — принят не северный (жилые от 2,5 м) (К-4); толщины стен приняты: наружные 250 мм, перегородки 120 мм — не обмерены (К-5); разрешённая мощность 15 кВт принята по типовой квартире, технических условий нет (К-6).

См. лист открытых вопросов (лист 6, записи К-4–К-6).

Примечания

1. Развёртки — вид на стену изнутри помещения, по часовой стрелке; расположение — на схеме листа и на листе 60; размеры — в мм по чистовым поверхностям; отметки — в м от ±0,000; высоты Н — от чистого пола помещения до оси изделия, у декора — до центра.
2. Красная цепочка — привязки электроточек и выводов по осям от угла чистовых стен; высота Н — у знака, от чистого пола до оси; высоты мебели, проёмов и границ отделки — колонкой отметок слева. Стена с 5 и более точками или с мелкими звеньями привязок показана двумя видами: архитектурная развёртка (мебель, отделка, проёмы, высоты) и вид «Привязки» на отдельном листе — точки и выводы с марками, одна цепочка по осям и таблица привязок (каждая точка — строка).
3. У знака электроточки: марка (Р — розетка, S — выключатель, Св — светильник, ЭВ — вывод кабеля), ×N — число постов в рамке, гр. — группа щита, Н — высота оси от чистого пола, мм; группы по клавишам выключателя — на листе выключателей.
4. Схема мебели, приборов и декора не является технической документацией для производства мебели; габариты — по паспортам изделий.
5. Двери скрытого монтажа — полотно в плоскости стены, отделка стены по полотну, плинтус прерывается у короба (узел — на листе узлов).

1000 мм · печать 1:1

Изм.	Кол.уч	Лист	№ док.	Подп.	Дата
Разраб.		Кырлан А.С.			04.11.26
Пров.					
ГИП					
Н. контр.					
Утв.					

ГД-2026-006-АИ

Квартира 58 м²

Общая площадь 55,23* м² · * размеры приняты, не замерены (реестр — л. 6, 7, К-5)

Дизайн-проект интерьера

Стадия	Лист	Листов
РП	79	87

Развёртка стены Г. Гардеробная (пом. 6)

М 1:20


Кырлан Александр Сергеевич

выпуск 04.11.2026 № 94e55e632e · стр. 87 из 96


Узлы

Пороги и стыки покрытий, скрытые двери, короба стояков, гидроизоляция, плинтус


1 **Порог 15 мм: мокрая зона — смежное помещение (М 1:5)**
Применение: двери Д-4; места — лист 60

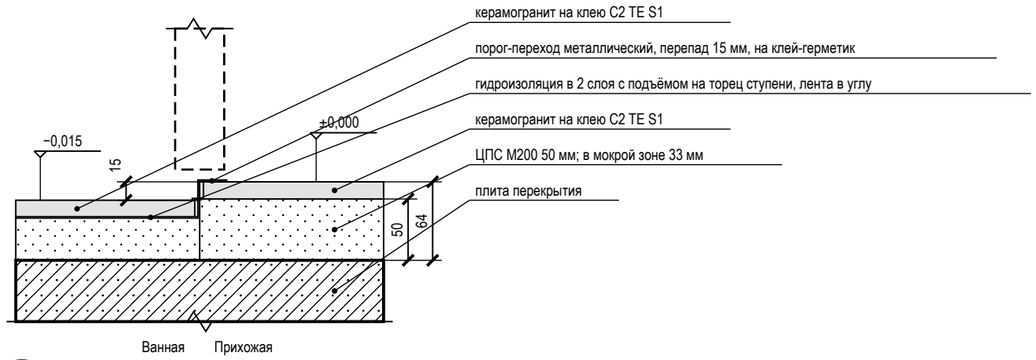


2 **Дверь скрытого монтажа в плоскости стены, плинтус (М 1:5)**
Применение: двери Д-2, Д-3, Д-4; места — лист 60

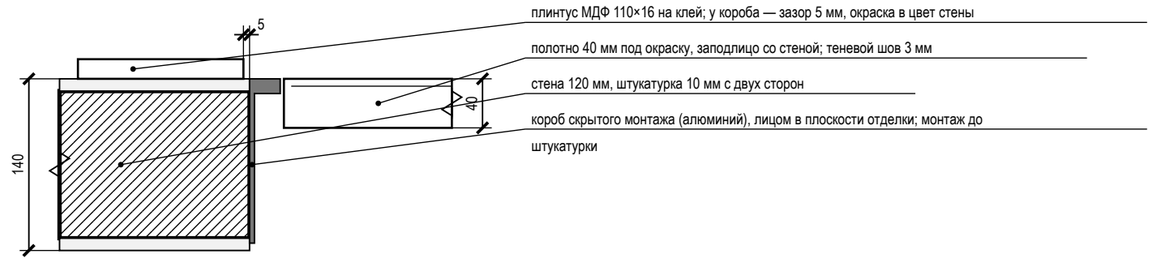


3 **Короб стояков К1-1 с люком и звукоизоляцией (М 1:10)**
Применение: пом. 3; места — лист 60

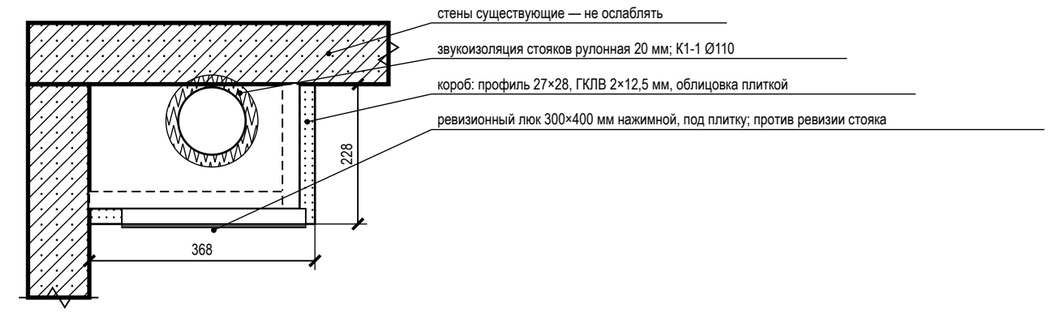


4 **Гидроизоляция санузла: заход на стены 200 мм, примыкание ванны (М 1:20)**
Применение: пом. 3, 4; места — лист 60

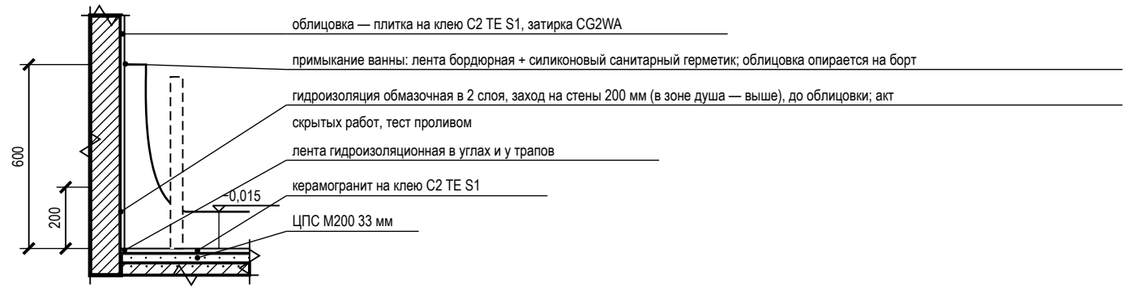

5 **Плинтус МДФ 110×16 мм у окрашенной стены по доске (ламинату) (М 1:10)**
Применение: пом. 1, 2, 6; места — лист 60

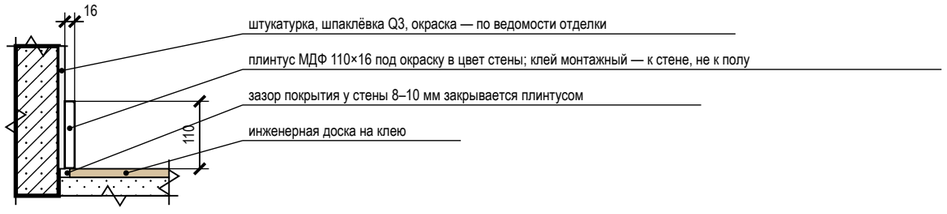

6 **Плинтус МДФ 110×16 мм у окрашенной стены по керамограниту (плитке) (М 1:10)**
Применение: пом. 5; места — лист 60

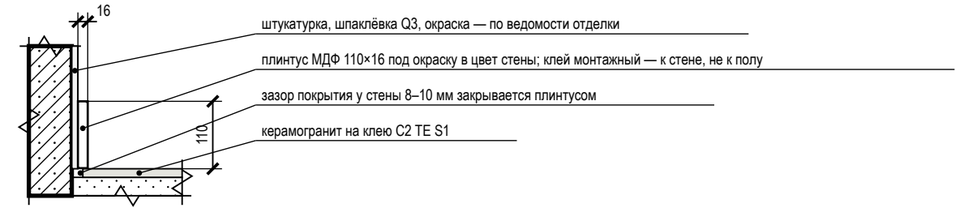

Условные обозначения

- железобетон (плита, стены) — условно: конструкция не установлена
- кладка, перегородка — условно: конструкция не установлена
- стяжка, раствор
- гипсокартон ГКЛВ
- звукоизоляция, эластичный заполнитель
- плитка, керамогранит на клею
- инженерная доска (покрытие пола)
- металлический профиль (порог, Т-профиль, короб двери)
- гидроизоляция (обмазочная, лента)

Примечания

1. Узлы — типовые решения проекта для мест, отмеченных выносками на листе схемы расположения развёрток и узлов; размеры — в мм, отметки — в м от ±0,000.
2. Узлы с гидроизоляцией, закладными и коробами скрытого монтажа принимаются по актам скрытых работ до закрытия отделкой; гидроизоляция — после теста проливом (24 ч).
3. Марки изделий (порог, Т-профиль, короб скрытой двери, люк) — по спецификациям; замена — на аналог с теми же габаритами по согласованию с автором проекта.
4. Материал плиты перекрытия и стен в узлах показан условно (железобетон, кладка): конструкция дома не установлена — крепёж, анкеры и толщины слоёв уточняются после обследования (до него — по допущениям общих указаний).

Допущения и предложения на листе. Основа листа: размеры сняты с плана заказчика, контрольный обмер не выполнен (К-5); высота потолка 2700 мм принята: на плане заказчика не указана (К-5); подрайон климата не задан — принят не северный (жилые от 2,5 м) (К-4); толщины стен приняты: наружные 250 мм, перегородки 120 мм — не обмерены (К-5); разрешённая мощность 15 кВт принята по типовой квартире, технических условий нет (К-6). См. лист открытых вопросов (лист 6, записи К-4–К-6).

Изм.	Кол.уч	Лист	№ док.	Подп.	Дата
Разраб.		Кырлан А.С.			04.11.26
Пров.					
ГИП					
Н. контр.					
Утв.					

ГД-2026-006-АИ

Квартира 58 м²

Общая площадь 55,23* м² · * размеры приняты, не замерены (реестр — л. 6, 7, К-5)

Дизайн-проект интерьера

Стадия	Лист	Листов
РП	80	87

Узлы

М 1:5; 1:10; 1:20

Кырлан Александр Сергеевич

выпуск 04.11.2026 № 94e55e632e · стр. 88 из 96

09

Смета

Кырлан Александр Сергеевич

выпуск 04.11.2026 № 94e55e632e · стр. 89 из 96

Ведомость объёмов работ

ПРЕДВАРИТЕЛЬНО · не для производства работ · открыто пунктов: 10 (реестр — л. 6, 7)

Объёмы по помещениям от чертежа · площади в м², длины в м · формула, правило проёмов и источник в каждой строке

Ведомость объёмов работ по помещениям

Поз.	Наименование работ (материал, число слоёв)	Ед. изм.	Объём по помещениям (№ по экспликации)						Всего	Формула подсчёта	Правило проёмов	Источник	Цена за ед., ₽	Стоимость, ₽
			1	2	3	4	5	6						
1. Демонтаж и черновые работы														
1	Демонтаж существующего покрытия пола до основания	м²	21,04	13,95	2,95	1,80	9,55	5,94	55,23	S пом.		л. 14, 15	по КП	
2	Демонтаж существующей отделки стен до основания	м²	41,25	33,91	16,94	14,12	22,66	24,67	153,55	P × H − проёмы	за вычетом проёмов	л. 14, 15	по КП	
3	Демонтаж существующей отделки потолка до основания	м²	21,04	13,95	2,95	1,80	9,55	5,94	55,23	S пом.		л. 14, 15	по КП	
4	Демонтаж существующих дверных блоков	шт					5	1	6	по ведомости проёмов		л. 15, 16	по КП	
5	Демонтаж существующих сантехприборов и электрооборудования (если есть)	компл								по факту на объекте		л. 15	по КП	
6	Устройство стяжки: стяжка ЦПС М200, 50 мм	м²	21,09	14,00	2,99	1,84	9,90	5,99	55,81	S пом. + S в дверных проёмах (b × t/2)	проёмы добавлены	л. 47, 48	530	29 579
7	Гидроизоляция обмазочная, 2 слоя: пол, стены на 200 мм, зоны замачивания	м²			4,22	2,85			7,07	пол + (P − двери) × h заведения + зоны замачивания		л. 43	450	3 182
8	Штукатурка стен по маякам, до 10 мм	м²						24,67	24,67	P × H − проёмы по обводу коробок − грани перегородок на ГКЛВ	за вычетом проёмов	л. 14, 48	530	13 075
9	Штукатурка оконных откосов шириной до 200 мм	м²	1,73	0,86					2,59	Σ (2h + b) × глубина откоса	откосы ≤ 200 мм	л. 14	540	1 399
10	Потолок ГКЛ по каркасу П113, 1 слой	м²	21,04	13,95	2,95	1,80	9,55		49,29	S пом. по плану потолков		л. 40–42	1 500	73 935
Итого по разделу 1 — 121 170 ₽ (позиций 10, из них по КП 5); в сводную смету — л. 86, 87														
2. Инженерные системы														
11	Прокладка слаботочной линии: Кабель домофона — тип по системе поставщика, отдельно от силовых	м							3,40	по лучам от ЩС**: 1 точ., запас 10 %		л. 26	по КП	
12	Прокладка слаботочной линии: Кабель коаксиальный RG-6 (75 Ом) к розеткам ТВ, отдельно от силовых	м							16,30	по лучам от ЩС**: 1 точ., запас 10 %		л. 26	по КП	
13	Прокладка слаботочной линии: Кабель U/UTP кат. 5e (LAN, Wi-Fi и камеры по PoE), отдельно от силовых	м							30,10	по лучам от ЩС**: 2 точ., запас 10 %		л. 26	по КП	
14	Прокладка гофротрубы Ø20 для слаботочных линий, отдельно от силовых	м							44,80	по длине лучей без участков в канале плинтуса (≈ 90 %)		л. 26	по КП	
15	Сборка слаботочного щита ЩС**: корпус, патч-панель, подключение линий и питания 220 В; коммутатор и точки доступа — оборудование заказчика	шт							1	один щит		л. 23, 26	по КП	
16	Электроточка: подрозетник в бетоне, розетка, выключатель, вывод	шт	16	6	3		7	1	33	по ведомости электроточек		л. 20, 23	950	31 350
17	Штробы в стенах под спуски кабеля к точкам — выполняются только после технического заключения о несущих стенах	м	30,00	11,70	3,35		12,15	1,80	59,00	Σ (H − h) по точкам на стенах: вертикальные спуски	после техзаключения	л. 15, 20	по КП	
18	Установка встраиваемого точечного светильника	шт			1	1	2		4	по плану освещения		л. 21	750	3 000
19	Монтаж светильника: потолочного, подвесного, настенного	шт	2	4	1			1	8	по плану освещения		л. 21	1 200	9 600
20	Монтаж LED-ленты в алюминиевый профиль	м	1,80						1,80	Σ длин лент по плану освещения		л. 21	230	414
21	Установка блока питания LED в доступном месте (люк, шкаф)	шт	1	1					2	один на LED-группу		л. 21	570	1 140
22	Установка автономного пожарного извещателя	шт	1	1			1		3	по плану розеток		л. 20	по КП	
23	Сборка щита: установка автоматов и АВДТ групп, вводного автомата	шт							7	группы + вводной автомат		л. 24	230	1 610

Допущения и предложения на листе

Основа листа: размеры сняты с плана заказчика, контрольный обмер не выполнен (К-5); высота потолка 2700 мм принята: на плане заказчика не указана (К-5); подрайон климата не задан — принят не северный (жилые от 2,5 м) (К-4); толщины стен приняты: наружные 250 мм, перегородки 120 мм — не обмерены (К-5); разрешённая мощность 15 кВт принята по типовой квартире, технических условий нет (К-6).

Знак «**» — предложение проектировщика, заказчиком не утверждено (согласовать с заказчиком): ЩС — щит слаботочный: место и состав.

См. лист открытых вопросов (лист 6, записи К-4–К-6).

Изм.	Кол.уч	Лист	№ док.	Подп.	Дата
Разраб.		Кырлан А.С.			04.11.26
Пров.					
ГИП					
Н. контр.					
Утв.					

ГД-2026-006-АИ

Квартира 58 м²

Общая площадь 55,23* м² · * размеры приняты, не замерены (реестр — л. 6, 7, К-5)

Дизайн-проект интерьера

Стадия	Лист	Листов
РП	81	87

Ведомость объёмов работ

М б/м

Кырлан Александр Сергеевич

выпуск 04.11.2026 № 94e55e632e · стр. 90 из 96

Ведомость объёмов работ (продолжение)

Объёмы по помещениям от чертежа · площади в м², длины в м · формула, правило проёмов и источник в каждой строке

Ведомость объёмов работ по помещениям (продолжение)

Поз.	Наименование работ (материал, число слоёв)	Ед. изм.	Объём по помещениям (№ по экспликации)						Всего	Формула подсчёта	Правило проёмов	Источник	Цена за ед., ₽	Стоимость, ₽
			1	2	3	4	5	6						
24	Установка вводного УЗО	шт							1	по однолинейной схеме		л. 24	380	380
25	Монтаж инсталляции, установка подвесного унитаза и кнопки смыва	шт				1			1	по плану выводов		л. 29, 38	10 500	10 500
26	Короб инсталляции: каркас и обшивка ГКЛВ в 2 слоя, ревизионный доступ к смыву	шт				1			1	по плану выводов		л. 29, 43–46	по КП	
27	Короб стояков Ш1 489 × 319 мм (внутренний 436 × 266): каркас и обшивка ГКЛВ в 2 слоя, ревизионный люк 300 × 400	м²			2,11				2,11	свободный периметр короба × H помещения		л. 14, 29	по КП	
28	Короб К1 над чистым полом: каркас и обшивка ГКЛВ под плитку (материалы — в спецификации ВК)	м.п.	0,40		0,76	0,30			1,46	Σ открытых участков выпусков К1 (профиль листа разводки ВК)		л. 29, 38	по КП	
29	Установка ванны с сифоном	шт			1				1	по плану выводов		л. 29, 38	6 000	6 000
30	Установка умывальника (мойки) с сифоном и смесителем	шт	1		1				2	по плану выводов		л. 29, 38	3 000	6 000
31	Подключение стиральной (посудомоечной) машины к ВК	шт	1						1	по плану выводов		л. 29	по КП	
32	Установка радиатора с узлом подключения и терморегулятором	шт	2	1					3	по плану отопления		л. 28	по КП	
Итого по разделу 2 — 69 994 ₽ (позиций 22, из них по КП 12); в сводную смету — л. 86, 87														
3. Чистовые работы														
33	Облицовка стен керамогранитом 1200×600 на клею	м²			14,95	13,40			28,35	по раскладке: зона облицовки − место за коробом	за вычетом проёмов	л. 43–46	2 500	70 875
34	Облицовка короба инсталляции (ГКЛВ) керамогранитом: лицо, боковины, полка	м²			1,99	1,47			3,46	по раскладке: лицо, боковины, полка		л. 43–46	2 500	8 650
35	Укладка керамогранита на пол, 600×600, на клею	м²			2,99	1,84	9,90		14,73	S пом. + S в дверных проёмах	проёмы добавлены	л. 43–47	1 800	26 514
36	Затирка швов керамогранита	м²			19,89	16,67	9,55		46,11	Σ S облицовки и пола из плитки		л. 43–46	150	6 917
37	Грунтование стен, 2 слоя (под штукатурку и под отделку)	м²	41,25	33,91	16,94	14,12	22,66	24,67	153,55	P × H − проёмы	за вычетом проёмов	л. 48	96	14 741
38	Шпаклёвка стен под окраску, 2 слоя (старт и финиш), уровень Q3	м²	41,25	33,91			22,66	24,67	122,49	P × H − проёмы − фартук	за вычетом проёмов	л. 48	750	91 868
39	Грунтование и шпаклёвка оконных откосов, 2 слоя	м.п.	9,60	4,80					14,40	Σ (2h + b) по окнам	по окнам	л. 14	300	4 320
40	Грунтование потолка, 2 слоя	м²	21,04	13,95	2,95	1,80	9,55	5,94	55,23	S пом.		л. 48	96	5 302
41	Шпаклёвка потолка под окраску, 2 слоя, уровень Q3	м²	21,04	13,95	2,95	1,80	9,55	5,94	55,23	S пом.		л. 40–42, 48	950	52 469
42	Окраска потолка водно-дисперсионной краской, 2 слоя	м²	21,04	13,95	2,95	1,80	9,55	5,94	55,23	S пом.		л. 48	360	19 883
43	Окраска стен водно-дисперсионной краской, 2 слоя	м²	48,26	38,15			32,74	26,35	145,50	P × H − фартук, проёмы не вычитаются	без вычета проёмов	л. 48	300	43 650
44	Окраска оконных откосов, 2 слоя	м.п.	9,60	4,80					14,40	Σ (2h + b) по окнам	по окнам	л. 14	120	1 728
45	Укладка инженерной доски на клей	м²	21,09	14,00				5,99	41,08	S пом. + S в дверных проёмах	проёмы добавлены	л. 47, 48	1 200	49 296
46	Установка плинтуса МДФ h=110 мм	м.п.	17,66	14,16			8,04	8,96	48,82	P − ширина дверных проёмов		л. 48	450	21 969
47	Окраска плинтуса в тоне S 0300-N, 2 слоя	м.п.	17,66	14,16			8,04	8,96	48,82	как плинтус		л. 48	300	14 646
48	Монтаж дверей скрытого монтажа под покраску (поставщик дверей)	шт					4	1	5	по ведомости проёмов		л. 16	5 250	26 250
49	Входная дверь, поставка с монтажом и откосами	шт							1	по ведомости проёмов		л. 16	по КП	
Итого по разделу 3 — 459 078 ₽ (позиций 17, из них по КП 1); в сводную смету — л. 86, 87														

Допущения и предложения на листе

Основа листа: размеры сняты с плана заказчика, контрольный обмер не выполнен (К-5); высота потолка 2700 мм принята: на плане заказчика не указана (К-5); подрайон климата не задан — принят не северный (жилые от 2,5 м) (К-4); толщины стен приняты: наружные 250 мм, перегородки 120 мм — не обмерены (К-5); разрешённая мощность 15 кВт принята по типовой квартире, технических условий нет (К-6).

См. лист открытых вопросов (лист 6, записи К-4–К-6).

Изм.	Кол.уч	Лист	№ док.	Подп.	Дата
Разраб.		Кырлан А.С.			04.11.26
Пров.					
ГИП					
Н. контр.					
Утв.					

ГД-2026-006-АИ

Квартира 58 м²

Общая площадь 55,23* м² · * размеры приняты, не замерены (реестр — л. 6, 7, К-5)

Дизайн-проект интерьера

Стадия	Лист	Листов
РП	82	87

Ведомость объёмов работ (продолжение)

М б/м

Кырлан Александр Сергеевич

Ведомость объёмов работ (окончание)

Объёмы по помещениям от чертежа · площади в м², длины в м · формула, правило проёмов и источник в каждой строке

Ведомость подсчёта площадей по помещениям

№	Помещение	S пола, м²	P, м	H, м	P × H, м²	Проёмы, м²	Стены нетто, м²	В дверных проёмах, м²	Плинтус, м	Откосы, м.п.
1	Кухня-гостиная	21,04	18,56	2,60	48,26	7,01	41,25	0,05	17,66	9,60
2	Спальня	13,95	14,96	2,55	38,15	4,24	33,91	0,05	14,16	4,80
3	Ванная	2,95	7,04	2,62	18,41	1,47	16,94	0,04	нет	нет
4	Санузел	1,80	5,96	2,62	15,59	1,47	14,12	0,04	нет	нет
5	Прихожая	9,55	12,84	2,55	32,74	10,08	22,66	0,35	8,04	нет
6	Гардеробная	5,94	9,76	2,70	26,35	1,68	24,67	0,05	8,96	нет
	Итого	**55,23**			**179,49**	**25,95**	**153,54**	**0,58**	**48,82**	**14,40**

Реестр контрольных сумм

Показатель	По ВОР	По чертежу	Расхождение	Лист
Σ площадей помещений без летних, м² — общая площадь по экспликации	55,23	55,23	0,0 %	л. 14
Стены под окраску, м² (шпаклёвка) ведомость отделки	122,49	122,49	0,0 %	л. 48
Потолки под окраску, м² — ведомость отделки	55,23	55,23	0,0 %	л. 48
Плинтус, м — ведомость отделки	48,82	48,82	0,0 %	л. 48
Плитка к заказу, шт — ведомость плитки	152	152	0,0 %	л. 43
Гидроизоляция, м² — ведомость материалов плитки	7,07	12,21	-42,1 %	л. 43
Точки ЭОМ, шт — планы ЭОМ (без щитов)	51	52	-1,9 %	л. 20, 21

Примечания

1. Объёмы — от геометрии проекта (та же, что на планах и в ведомости отделки), не от общей площади: P — периметр чистого контура, H — от чистого пола до низа потолка, проёмы — по наружному обводу коробок.
2. Подсчёт по ГЭСН-2001-15 и ГЭСН-2001-11: штукатурка и шпаклёвка стен — за вычетом проёмов; окраска водными составами — без вычета проёмов (п. 2.24); откосы — отдельно, по ширине до 200 и более 200 мм; полы — с площадью в дверных проёмах.
3. Плитка — по раскладке (целые и с подрезкой); короб инсталляции и фартук — отдельными строками, двойного счёта облицовки нет. Материалы, запас и количество к заказу — в спецификации материалов.
4. Цены — ориентир по открытым прайсам Москвы (цены на 21.09.2026), не коммерческое предложение; «по КП» — расценки нет, строка в итог не входит.
5. Демонтаж — по плану демонтажа и общим указаниям: покрытия пола, отделка стен и потолков, дверные блоки — до основания; объёмы справочные — по плану демонтажа (расценки в книге нет — «по КП»).
6. Штробы в стенах — только после технического заключения о несущих стенах (общие указания, план обмера и демонтажа): строка «Штробы в стенах» вертикальные спуски кабеля от потолочной трассы к точкам, объём не меньше фактического (горизонтальные трассы — по исполнительной схеме). Расценки штробления в прайсе нет — «по КП», в итог не входит; кабель в штробах стен прокладывается после неё.
7. Слаботочные сети: кабель по лучам от ЩС** 49,80 м (U/UTP, RG-6, домофон — по видам), гофра 44,80 м, щит ЩС** с патч-панелью; розетки RJ45 и ТВ монтируются в строке «Электроточка». Длины те же, что в ведомости изделий электрика (одна модель — lowcurrent-engineer/bom.js); оборудование заказчика (точки доступа, камеры, коммутатор) в спецификацию не входит.
8. Коробы: стояков (Ш1 — 2,11 м²) и К1 над чистым полом (1,45 м открытых участков; труба К1 вдоль стен 11,22 м в короб не зашивается — она за приборами, в раме инсталляции и в шахтах). В спецификации ВК короб К1 заказывается с запасом 10 % — 1,60 м. Материалы коробов стояков и инсталляции — в спецификации материалов, К1 — в спецификации ВК.

Допущения и предложения на листе

Основа листа: размеры сняты с плана заказчика, контрольный обмер не выполнен (К-5); высота потолка 2700 мм принята: на плане заказчика не указана (К-5); подрайон климата не задан — принят не северный (жилые от 2,5 м) (К-4); толщины стен приняты: наружные 250 мм, перегородки 120 мм — не обмерены (К-5); разрешённая мощность 15 кВт принята по типовой квартире, технических условий нет (К-6).

Знак «**» — предложение проектировщика, заказчиком не утверждено (согласовать с заказчиком): ЩС — щит слаботочный: место и состав.

См. лист открытых вопросов (лист 6, записи К-4–К-6).

Изм.	Кол.уч	Лист	№ док.	Подп.	Дата
Разраб.		Кырлан А.С.			04.11.26
Пров.					
ГИП					
Н. контр.					
Утв.					

ГД-2026-006-АИ

Квартира 58 м²

Общая площадь 55,23* м² · * размеры приняты, не замерены (реестр — л. 6, 7, К-5)

Дизайн-проект интерьера

Стадия	Лист	Листов
РП	83	87

Ведомость объёмов работ (окончание)

М б/м

Кырлан Александр Сергеевич

Спецификация материалов

ПРЕДВАРИТЕЛЬНО · не для производства работ · открыто пунктов: 10 (реестр — л. 6, 7)

Отделочные материалы: чистое количество, запас, упаковка, к заказу · ГОСТ 21.110-2013

Спецификация материалов (ГОСТ 21.110-2013, форма 1)

Поз.	Наименование и техническая характеристика	Тип, марка, артикул	Код продукции	Поставщик	Ед. изм.	Количество				Масса ед., кг	Примечание
						чистое	запас, %	упаковка	к заказу		
Покрытия полов и облицовка											
1	Инженерная доска (дуб натуральный, рабочий слой 4 мм, эмиссия E1, прямая укладка)	аналог: инженерная доска, дуб натуральный, масло, 1-полосная, 14/4 мм			м²	41,08	7	по артикулу	44,00 м²		пом. 1, 2, 6; до целой упаковки; л. 47, 48
2	Клей для паркетной и инженерной доски (эластичный, по ТУ изготовителя доски)	по выбору подрядчика			м²	41,08		ведро по ТУ	по ТУ		расход кг/м² — по ТУ клея; л. 47
3	Керамогранит 600×600 мм SG651622R	SG651622R			шт	48	10	коробка	54 шт		12 целых + 36 с подрезкой; 14,30 м² по раскладке, к заказу 19,44 м²; пом. 3, 4, 5; л. 43–46
4	Керамогранит 1200×600 мм 610015000370	610015000370			шт	87	10	коробка	98 шт		0 целых + 87 с подрезкой; 31,81 м² по раскладке, к заказу 70,56 м²; пом. 3, 4; л. 43–46
Сухие смеси и гидроизоляция											
5	Клей плиточный цементный класса C2 S1 (ГОСТ Р 56387-2018)	по выбору подрядчика			кг	31,17	10	мешок 25 кг	2 меш.	25	слой 5 мм, 1,50 кг/м² на 1 мм; л. 43
6	Клей плиточный цементный класса C2 (ГОСТ Р 56387-2018)	по выбору подрядчика			кг	301,17	10	мешок 25 кг	14 меш.	25	слой 5 мм, 1,50 кг/м² на 1 мм; л. 43
7	Затирка цементная класса класс не задан, цвет — по колерной карте	по выбору подрядчика			кг	3,51	10	упак. 2 кг	2 упак.	2	расход (a+b)/ab × шов × t × 1,6 кг/м²; л. 43
8	Гидроизоляция обмазочная полимерная, 2 слоя, лента в углах, манжеты на выводах	по выбору подрядчика			м²	7,07	10	ведро по ТУ	по ТУ		пом. 3, 4; расход кг/м² — по ТУ; л. 43
9	Лента демпферная по периметру пола из плитки	по выбору подрядчика			м	19,14	10	рулон	22,00 м		л. 43
10	Смесь цементно-песчаная для стяжки М200 (50 мм, 33 мм)	по выбору подрядчика			м³	2,71	5	мешок по ТУ	по ТУ		S 55,81 м² × толщина; армирование и маяки — по ТУ; л. 47
11	Смесь штукатурная гипсовая для машинного и ручного нанесения по маякам, слой до 10 мм	по выбору подрядчика			м²	24,67	10	мешок по ТУ	по ТУ		пом. 6; расход кг/м² на 1 мм слоя — по ТУ смеси, толщина — по замеру кривизны стен; л. 14, 48
Короба из ГКЛВ											
12	Лист ГКЛВ 12,5 мм, 2500 × 1200 мм, обшивка коробов в 2 слоя	по выбору подрядчика			м²	4,22	10	лист 3,00 м²	2,00 лист		короб Ш1 пом. 3: 2,11 м²; площадь × 2 слоя; короб К1 над полом — в спецификации ВК; л. 29, 43–46
13	Профиль стальной оцинкованный 27 × 28 мм: каркас коробов (стойки и направляющие)	по выбору подрядчика			м	12,08	10	хлыст 3 м	5 шт		стойки через 400 мм по свободному периметру + направляющие по полу и потолку; крепёж, лента, шпаклёвка швов — по узлу короба; л. 29, 43–46
Слаботочные сети											
14	Кабель домофона — тип по системе поставщика	по выбору подрядчика			м	3,40		бухта по ТУ	4,00 м		по лучам от ЩС**, 1 точ., запас 10 % уже в длине; л. 26
15	Кабель коаксиальный RG-6 (75 Ом) к розеткам ТВ	по выбору подрядчика			м	16,30		бухта по ТУ	17,00 м		по лучам от ЩС**, 1 точ., запас 10 % уже в длине; л. 26
16	Кабель U/UTP кат. 5e (LAN, Wi-Fi и камеры по PoE)	по выбору подрядчика			м	30,10		бухта по ТУ	31,00 м		по лучам от ЩС**, 2 точ., запас 10 % уже в длине; л. 26
17	Гофротруба Ø20 для слаботочных линий, отдельно от силовых	по выбору подрядчика			м	44,80		бухта по ТУ	45,00 м		по длине лучей без участков в канале плинтуса (≈ 90 %); л. 26
18	Розетка компьютерная RJ45, кат. 6, с рамкой и подрозетником	по выбору подрядчика			шт	2		шт	2 шт		LAN1, LAN2; серия механизмов — как у розеток и выключателей; л. 23, 26

Допущения и предложения на листе

Основа листа: размеры сняты с плана заказчика, контрольный обмер не выполнен (К-5); высота потолка 2700 мм принята: на плане заказчика не указана (К-5); подрайон климата не задан — принят не северный (жилые от 2,5 м) (К-4); толщины стен приняты: наружные 250 мм, перегородки 120 мм — не обмерены (К-5); разрешённая мощность 15 кВт принята по типовой квартире, технических условий нет (К-6).

Знак «**» — предложение проектировщика, заказчиком не утверждено (согласовать с заказчиком): ЩС — щит слаботочный: место и состав; пол пом. 1, 2, 6 — артикул изделия не выбран: позиция описана характеристиками («аналог по характеристикам»), артикул выбирается при закупке.

См. лист открытых вопросов (лист 6, записи К-4–К-6).

Изм.	Кол.уч	Лист	№ док.	Подп.	Дата
Разраб.		Кырлан А.С.			04.11.26
Пров.					
ГИП					
Н. контр.					
Утв.					

ГД-2026-006-АИ

Квартира 58 м²

Общая площадь 55,23* м² · * размеры приняты, не замерены (реестр — л. 6, 7, К-5)

Дизайн-проект интерьера

Стадия	Лист	Листов
РП	84	87

Спецификация материалов

М б/м

Кырлан Александр Сергеевич

Спецификация материалов (окончание)

ПРЕДВАРИТЕЛЬНО · не для производства работ · открыто пунктов: 10 (реестр — л. 6, 7)

Отделочные материалы: чистое количество, запас, упаковка, к заказу · ГОСТ 21.110-2013

Спецификация материалов (ГОСТ 21.110-2013, форма 1) (продолжение)

Поз.	Наименование и техническая характеристика	Тип, марка, артикул	Код продукции	Поставщик	Ед. изм.	Количество				Масса ед., кг	Примечание
						чистое	запас, %	упаковка	к заказу		
19	Розетка телевизионная (коаксиальная) с рамкой и подрозетником	по выбору подрядчика			шт	1		шт	1 шт		ТВ1; серия механизмов — как у розеток и выключателей; л. 23, 26
20	Трубка или монитор домофона (поставка домофонной организации)	по выбору подрядчика			шт	1		шт	1 шт		ДФ1; серия механизмов — как у розеток и выключателей; л. 23, 26
21	Щит слаботочный ЩС**: корпус, DIN-рейка, розетки 220 В	по выбору подрядчика			шт	1		шт	1 шт		ЩС**; серия механизмов — как у розеток и выключателей; л. 23, 26
22	Патч-панель, портов не менее 2	по выбору подрядчика			шт	1		шт	1 шт		серия механизмов — как у розеток и выключателей; л. 23, 26
Лакокрасочные материалы											
23	Краска интерьерная акриловая, полуматовая, класс истирания 1	Tikkurila S 1002-Y50R			л	9,90	10	банка 2,7 л	5 банк		41,25 м² × 2 сл. × 0,12 л/м²; пом. 1; л. 48
24	Краска интерьерная водно-дисперсионная, глубокоматовая, класс истирания 1	Tikkurila S 0300-N			л	11,83	10	банка 2,7 л	5 банк		49,29 м² × 2 сл. × 0,12 л/м²; пом. 1 (пот.), 2 (пот.), 3 (пот.), 4 (пот.), 5 (пот.); л. 48
25	Краска интерьерная акриловая, глубокоматовая, класс истирания 2	Tikkurila S 1502-Y50R			л	8,14	10	банка 2,7 л	4 банк		33,91 м² × 2 сл. × 0,12 л/м²; пом. 2; л. 48
26	Краска интерьерная акриловая, полуматовая, класс истирания 1	Tikkurila S 1502-Y50R			л	5,44	10	банка 2,7 л	3 банк		22,66 м² × 2 сл. × 0,12 л/м²; пом. 5; л. 48
27	Краска интерьерная акриловая, матовая, класс истирания 1	Tikkurila Harmony V503 «Winter»			л	5,92	10	банка 2,7 л	3 банк		24,67 м² × 2 сл. × 0,12 л/м²; пом. 6; л. 48
28	Краска интерьерная акриловая, глубокоматовая, класс истирания 2	Tikkurila Anti-Reflex 2 V503 «Winter»			л	1,43	10	банка 2,7 л	1 банк		5,94 м² × 2 сл. × 0,12 л/м²; пом. 6 (пот.); л. 48
29	Шпаклёвка финишная полимерная под окраску (стены и потолки, Q3)	по выбору подрядчика			м²	177,72	10	ведро по ТУ	по ТУ		расход кг/м² на слой — по ТУ; л. 48
30	Грунтовка акриловая глубокого проникновения, 2 слоя	по выбору подрядчика			м²	208,78	10	канистра по ТУ	по ТУ		расход л/м² — по ТУ; л. 48
Погонажные изделия и потолки											
31	Плинтус напольный МДФ под покраску, h=110 мм, крепление к стене	SX184			м.п.	48,82	10	хлыст 2,4 м	23 шт		пом. 1, 2, 5, 6; длина хлыста — по артикулу; л. 48
32	Потолок подвесной ГКЛ/ГКЛВ по каркасу Knauf П113: листы, профили, подвесы, лента, шпаклёвка швов	Knauf П113			м²	49,29		комплект	по л. потолков		площадь — по ведомости потолков; число листов, профилей и подвесов — по шагам каркаса на листе потолков; л. 40–42

Примечания

1. Чистое количество — из ведомости объёмов работ и раскладки плитки; запас — отдельной графой (доска — по ведомости отделки, плитка, краска и плинтус — 10 %); «к заказу» — с запасом и кратно упаковке.
2. Плитка — штуками по раскладке, запас на каждую поверхность. Калибр (рабочий размер) и тон — одной партией на помещение, калибр указать при заказе и сверить с раскладкой до укладки.
3. Краска — 0,12 л/м² на слой (середина вилки 0,10–0,15 л/м²) по фактической площади окраски из ведомости отделки; колеровка одной партией.
4. «По ТУ» — расход задаёт производитель выбранного продукта; количество к заказу — после выбора марки.
5. Поз. 1 заданы характеристиками («аналог:»): марку, артикул и поставщика согласовать с заказчиком до закупки, без артикула не заказывать.
6. Штукатурная смесь — на ту же площадь, что строка ВОР «Штукатурка стен» (24,67 м²): площадь одна, расход смеси задаёт производитель.
7. Коробы инсталляции и стояков: ГКЛВ в 2 слоя и профиль 27 × 28 мм считаются по свободным граням коробов (источник — раскладка плиточника и шахты в данных); короб К1 над полом — в спецификации ВК.
8. Потолки ГКЛ: в этой спецификации — площадь системы П113; число листов, профилей и подвесов — по шагам каркаса на листе потолков (подвесы через 1000, несущие через 500, основные через 1200 мм), схема каркаса не выпущена. Сантехника, светильники и мебель — по своим спецификациям.

Допущения и предложения на листе

Основа листа: размеры сняты с плана заказчика, контрольный обмер не выполнен (К-5); высота потолка 2700 мм принята: на плане заказчика не указана (К-5); подрайон климата не задан — принят не северный (жилые от 2,5 м) (К-4); толщины стен приняты: наружные 250 мм, перегородки 120 мм — не обмерены (К-5); разрешённая мощность 15 кВт принята по типовой квартире, технических условий нет (К-6).

Знак «**» — предложение проектировщика, заказчиком не утверждено (согласовать с заказчиком): ЩС — щит слаботочный: место и состав; пол пом. 1, 2, 6 — артикул изделия не выбран: позиция описана характеристиками («аналог по характеристикам»), артикул выбирается при закупке.

См. лист открытых вопросов (лист 6, записи К-4–К-6).

Изм.	Кол.уч	Лист	№ док.	Подп.	Дата
Разраб.		Кырлан А.С.			04.11.26
Пров.					
ГИП					
Н. контр.					
Утв.					

ГД-2026-006-АИ

Квартира 58 м²

Общая площадь 55,23* м² · * размеры приняты, не замерены (реестр — л. 6, 7, К-5)

Дизайн-проект интерьера

Стадия	Лист	Листов
РП	85	87

Спецификация материалов (окончание)

М б/м

Кырлан Александр Сергеевич

Смета ориентировочная

ПРЕДВАРИТЕЛЬНО · не для производства работ · открыто пунктов: 10 (реестр — л. 6, 7)

Работы, материалы, оборудование, услуги и резерв · цены — ориентир по открытым прайсам, не коммерческое предложение

Сводная смета (цены на 21.09.2026, Москва)

№	Наименование работ, материалов, услуг	Ед. изм.	Кол-во	Цена за ед., ₽	Стоимость, ₽			Чей подряд	Срок поставки, дн.	Основание	Источник цены
					план	факт	разница				
Работы — по ведомости объёмов работ											
1	Демонтаж и черновые работы (без 5 поз. по КП)	раздел	1		121 170			бригада		ВОР, поз. 1–10; л. 81–83	по ВОР
2	Инженерные системы (без 12 поз. по КП)	раздел	1		69 994			бригада		ВОР, поз. 11–32; л. 81–83	по ВОР
3	Чистовые работы (без 1 поз. по КП)	раздел	1		459 078			бригада, поставщик		ВОР, поз. 33–49; л. 81–83	по ВОР
Материалы — по спецификации материалов											
4	Инженерная доска	м²	44,00	4 513	198 572			поставщик		спецификация, поз. 1	Ц7
5	Керамогранит 600×600 мм	м²	19,44	1 800	34 992			поставщик		спецификация, поз. 3	Ц6
6	Керамогранит 1200×600 мм	м²	70,56	3 500	246 960			поставщик		спецификация, поз. 4	Ц6
7	Клей плиточный цементный класса C2 S1	меш.	16	1 800	28 800			поставщик		спецификация, поз. 5, 6	Ц7
8	Краска Tikkurila (Harmony, Anti-Reflex 2), банка 2,7 л	банк	21	3 510	73 710			поставщик		спецификация, поз. 23, 24, 25, 26, 27, 28	Ц6
9	Плинтус напольный МДФ под покраску	шт	23	368	8 464			поставщик		спецификация, поз. 31	Ц7
10	Прочие материалы с расходом по ТУ (клей для доски, затирка, гидроизоляция, демпферная лента, смесь для стяжки, смесь штукатурная гипсовая для машинного и ручного нанесения по маякам, лист гклв 12, профиль стальной оцинкованный 27 × 28 мм: каркас коробов (стойки и направляющие), кабель слаботочки, гофра слаботочки, изделия слаботочки, шпаклёвка, грунтовка, каркас и ГКЛ потолков)	компл	1	по КП				поставщик		спецификация, поз. 2, 7, 8, 9, 10, 11, 12, 13, 14, 15, 16, 17, 18, 19, 20, 21, 22, 29, 30, 32	
Оборудование и мебель — поставка по спецификациям											
11	Кухонный гарнитур по проекту кухни, изготовление и монтаж (4–8 нед.)	компл	1	по КП				поставщик	не задан; ориентир 4–8 нед. от замера	л. 55, 56	
12	Двери скрытого монтажа с коробом под покраску, поставка	шт	5	по КП				поставщик	не задан; ориентир ≈ 30 дн.	л. 16	

Допущения и предложения на листе

Основа листа: размеры сняты с плана заказчика, контрольный обмер не выполнен (К-5); высота потолка 2700 мм принята: на плане заказчика не указана (К-5); подрайон климата не задан — принят не северный (жилые от 2,5 м) (К-4); толщины стен приняты: наружные 250 мм, перегородки 120 мм — не обмерены (К-5); разрешённая мощность 15 кВт принята по типовой квартире, технических условий нет (К-6).

См. лист открытых вопросов (лист 6, записи К-4–К-6).

Изм.	Кол.уч	Лист	№ док.	Подп.	Дата
Разраб.		Кырлан А.С.			04.11.26
Пров.					
ГИП					
Н. контр.					
Утв.					

ГД-2026-006-АИ

Квартира 58 м²

Общая площадь 55,23* м² · * размеры приняты, не замерены (реестр — л. 6, 7, К-5)

Дизайн-проект интерьера

Стадия	Лист	Листов
РП	86	87

Смета ориентировочная

М б/м

Кырлан Александр Сергеевич

Смета ориентировочная (окончание)

Работы, материалы, оборудование, услуги и резерв · цены — ориентир по открытым прайсам, не коммерческое предложение

Сводная смета (цены на 21.09.2026, Москва) (продолжение)

№	Наименование работ, материалов, услуг	Ед. изм.	Кол-во	Цена за ед., ₽	Стоимость, ₽			Чей подряд	Срок поставки, дн.	Основание	Источник цены
					план	факт	разница				
13	Оборудование заказчика слаботочных сетей: коммутатор — 1 шт	компл	1	по КП				заказчик		л. 23	
14	Сантехника, светильники, мебель и предметы интерьера	компл	1	по КП				поставщик		л. 38; л. 39; л. 58; л. 19	
Прочие работы и услуги											
15	Вынос и вывоз строительного мусора	м³		по факту				бригада		после демонтажа	
16	Подъём материалов на этаж (лифтом или вручную — по договору)	т		по факту				бригада		по массе поставки	
17	Доставка чистовых материалов, 10 % от поставки			10 %	59 150			поставщик		от суммы материалов	
18	Уборка после ремонта	м²	55,23	по факту				бригада		S квартиры	
	Итого работы				**650 242**						
	Итого материалы				**591 498**						
	Итого прочие услуги				**59 150**						
	Резерв на непредвиденные работы и материалы, 15 %				**195 134**						
	ВСЕГО ориентировочно (без оборудования и позиций по КП)				**1 496 024**						

Примечания

1. Смета ориентировочная, не коммерческое предложение: объёмы — из ведомости объёмов работ и спецификации материалов, цены — нижняя граница открытых прайсов Москвы (цены на 21.09.2026); перед договором цены подтвердить у подрядчика и поставщиков.
2. Источники цен: Ц1 — Домашний мастерок: прайс на отделочные работы, 2026; Ц2 — Домашний мастерок: прайс на плиточные работы, 2026; Ц3 Домашний мастерок: прайс на электромонтажные работы, 2026; Ц4 — Профи ремонтник: штукатурно-малярные работы; Ц5 — Profi.ru: укладка керамогранита на стены, Москва 2026; Ц6 — knowledge/spec-materials.md, разд. 1 и 3: ориентир по сегментам; Ц7 — Розница Москвы, 09.2026: Лемана ПРО, KGSnab, официальный дилер Farrow & Ball.
3. В итог не вошли позиции «по КП» и «по факту»: оборудование и мебель, двери, материалы с расходом по ТУ, вывоз мусора, подъём и уборка.
4. Доставка — 10 % от материалов, резерв — 15 % (частный ремонт 10–20 %) отдельными строками, в количествах не спрятаны. Графы «факт» и «разница» заполняются по актам.

Допущения и предложения на листе

Основа листа: размеры сняты с плана заказчика, контрольный обмер не выполнен (К-5); высота потолка 2700 мм принята: на плане заказчика не указана (К-5); подрайон климата не задан — принят не северный (жилые от 2,5 м) (К-4); толщины стен приняты: наружные 250 мм, перегородки 120 мм — не обмерены (К-5); разрешённая мощность 15 кВт принята по типовой квартире, технических условий нет (К-6).

См. лист открытых вопросов (лист 6, записи К-4–К-6).

Изм.	Кол.уч	Лист	№ док.	Подп.	Дата
Разраб.		Кырлан А.С.			04.11.26
Пров.					
ГИП					
Н. контр.					
Утв.					

ГД-2026-006-АИ

Квартира 58 м²

Общая площадь 55,23* м² · * размеры приняты, не замерены (реестр — л. 6, 7, К-5)

Дизайн-проект интерьера

Стадия	Лист	Листов
РП	87	87

Смета ориентировочная (окончание)

М б/м

Кырлан Александр Сергеевич