
L

LINEA

ДИЗАЙН-ПРОЕКТ ИНТЕРЬЕРА

# Квартира с кабинетом

*современный модерн*

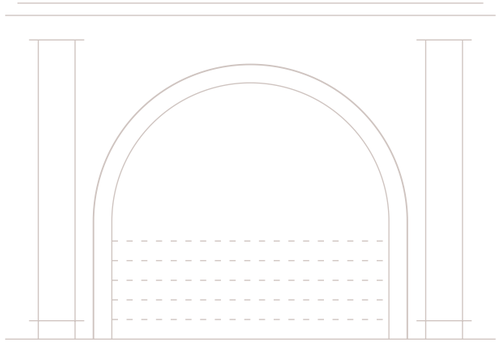


ПАЛИТРА ОТДЕЛКИ

| F&B No. 15 | V503 | F&B No. 34 | NCS S 2010-Y30 | NCS S 5020-G50 |
|---|---|---|---|---|
| 49 % | 41 % | 9 % | текстиль, декор | текстиль, декор |

АВТОР ПРОЕКТА

Кырлан Александр Сергеевич

Ноябрь 2026

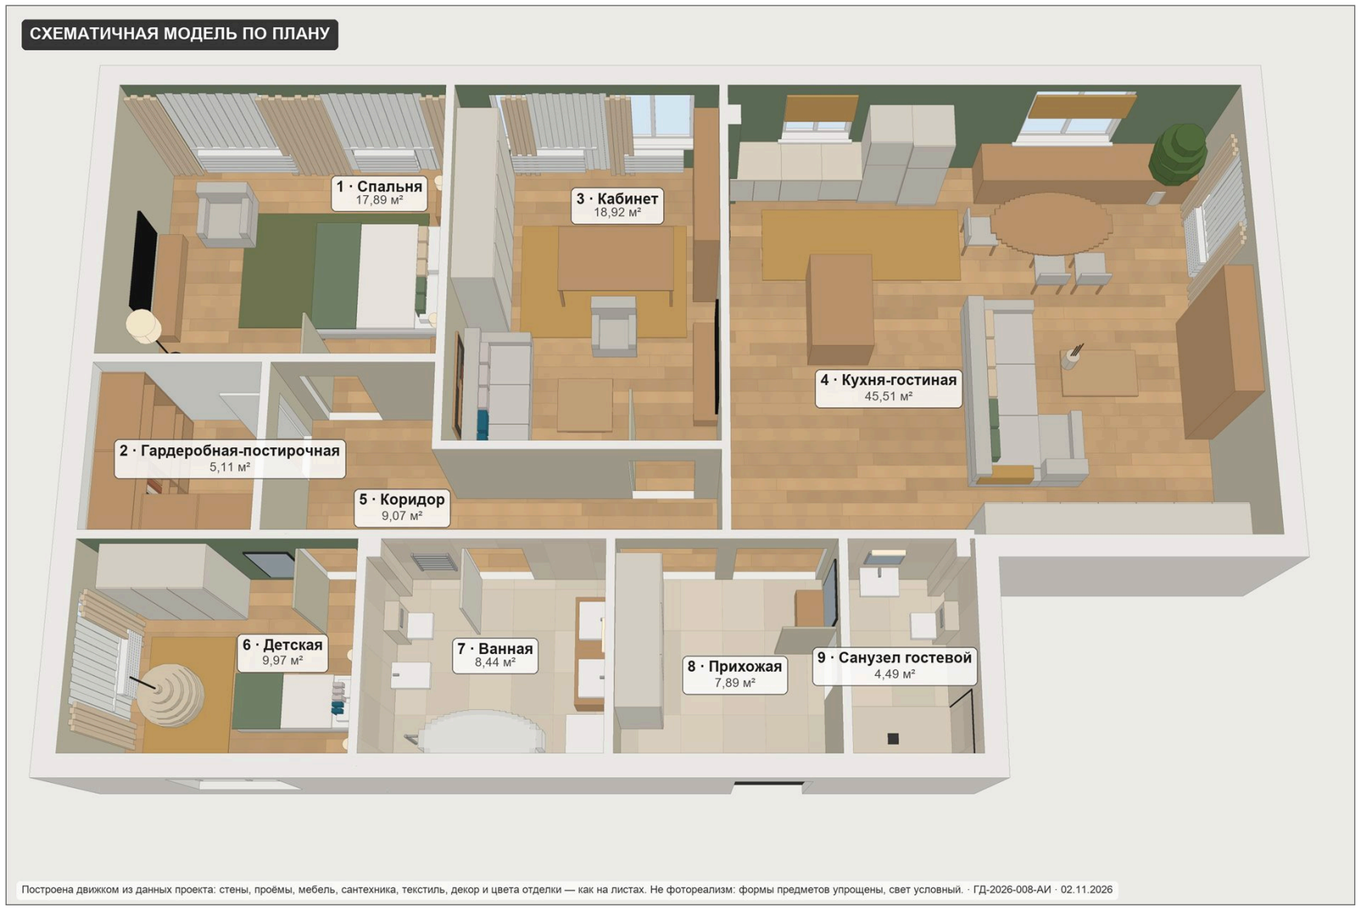



Квартира сверху · схематичная модель по плану

| ОБЩАЯ ПЛОЩАДЬ | ПОМЕЩЕНИЙ | СТАДИЯ | ШИФР | ОСНОВА |
|---|---|---|---|---|
| 127,29 м² | 9, из них жилых 4 | Проект · предварительно | ГД-2026-008-АИ | план заказчика, без обмера |

Как оставить правку: кнопка «Правка к этому листу» в правом верхнем углу любого листа · все листы проекта: дизайн-студия-квартир.рф/review.html?p=gost-modern4k

выпуск 04.11.2026 № 627e1ac6ce · стр. 1 из 127

# СХЕМАТИЧНАЯ МОДЕЛЬ ПО ПЛАНУ

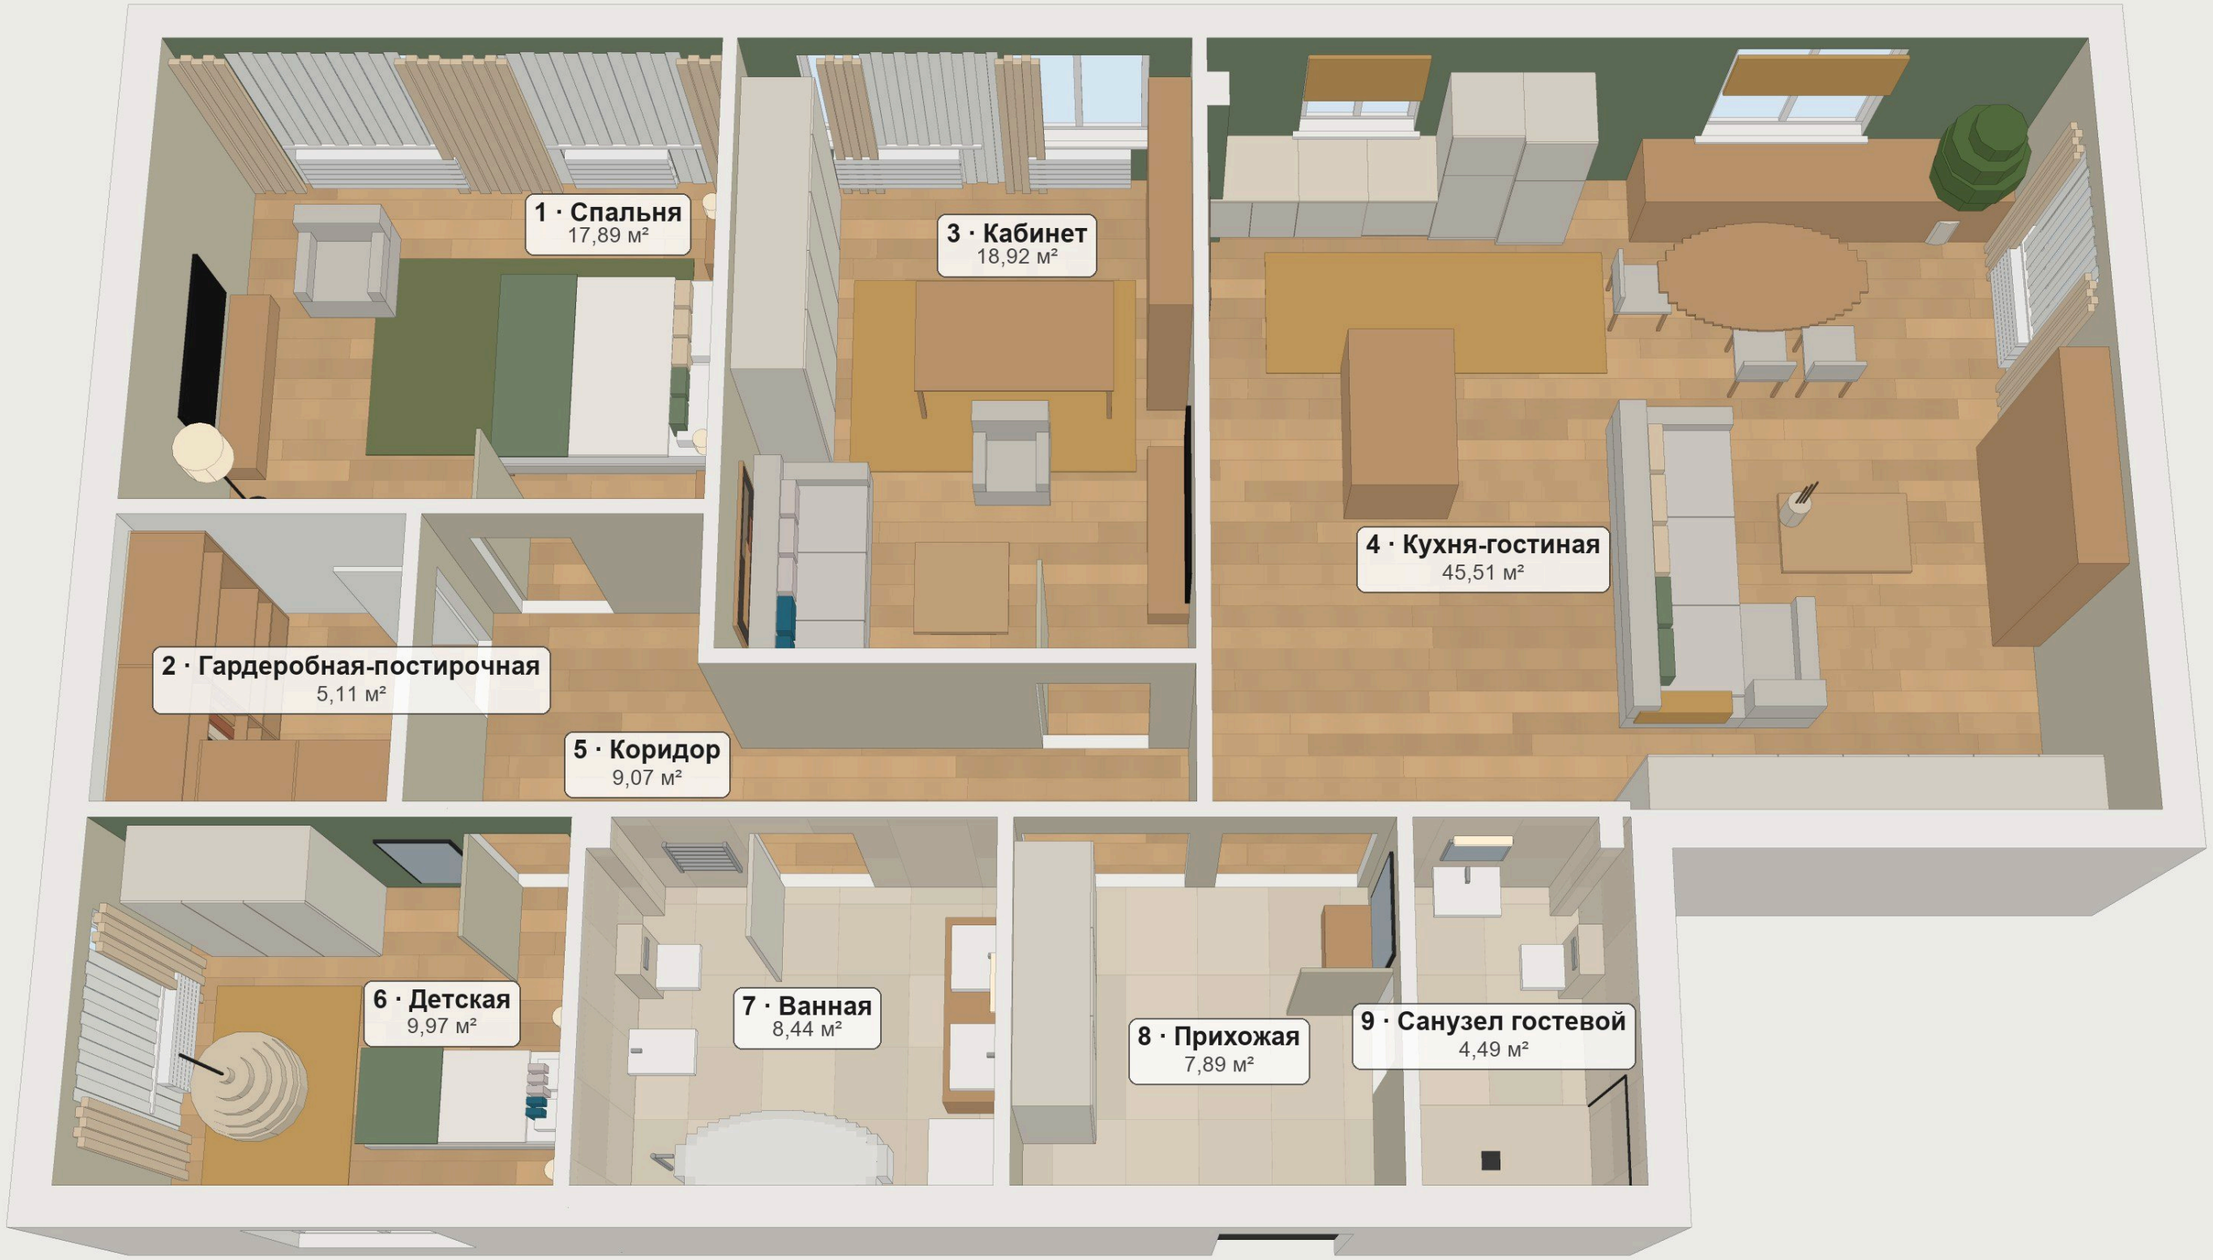


Построена движком из данных проекта: стены, проёмы, мебель, сантехника, текстиль, декор и цвета отделки — как на листах. Не фотореализм: формы предметов упрощены, свет условный. · ГД-2026-008-АИ · 02.11.2026

| | | | | | |
|---|---|---|---|---|---|
| | | | | | Проект: Квартира с кабинетом |
| | Лист | № док. | Подпись | Дата | |
| Дизайнер | Кырлан А.С. | | | 04.11.26 | Визуализация. Вид сверху |

| Стадия | Лист | Листов |
|---|---|---|
| П | 2 | 127 |

выпуск 04.11.2026 № 627e1ac6ce · стр. 2 из 127

## Объект

Квартира с кабинетом: 127,29 м², помещений 9, из них жилых 4.

Стиль: модерн (ар-нуво) 60 %, современный (контемпорари) 40 %. Стадия: предварительный альбом без обмера, планировка по плану заказчика.

Открытых вопросов 13, конфликтов разделов 0; изменений утверждено 9, ждут подписи 0.

## Розетки и выводы

41 розетка (рамок 34), 7 выводов кабеля под технику и свет, 14 групп щита — всё с высотами от чистого пола: листы 63, 64, 65.

## Что решено (подписано вами)

ИЗ-1 — M_30 — фасад МДФ 10 мм, эмаль матовая, профиль латунь матовая, зеркальные арочные вставки (поле 100 мм), как на кадре.

ИЗ-2 — Проём Д-6 сдвинут вдоль стены А от угла Б: привязка 2300 → 1200 (x 4900…5700), петли у x 4900, открывание внутрь, в сторону стены Г (там полотенцесушитель С_06 на стене А…

ИЗ-3 — M_05 переставлено в угол у окна 1 (x 600…1350, y 600…1350), столик M_04 свободен.

ИЗ-4 — Мебель кабинета — M_08, M_09, M_10, M_11, M_12, M_13, ОБ_02, мебель прихожей — M_30 (шкаф-купе), M_31 (банкетка).

ИЗ-5 — M_24 — каркас из оцинкованного профиля на стене Б с облицовкой панелями МДФ 19 мм, эмаль.

ИЗ-6 — РО-5 — на свободном участке наружной стены А между колонной M_14 и банкеткой M_20: привязка 3350, 500×600, низ +120 (x 11750…12250).

ИЗ-7 — РО-6 — низкий панельный прибор 1400×200 по ширине окна 2 (привязка 4400, низ +120, верх +320).

ИЗ-8 — Островная потолочная вытяжка 900 мм над M_19 в режиме рециркуляции (угольный фильтр), низ +1550.

ИЗ-9 — Биокамин в ТВ-стене M_24 остаётся, ниша 900×400, низ +350, облицовка негорючая (сталь 2 мм / камень), зазоры 50 мм до панелей.

## Что ждёт вашего ответа

К-1 — Размеры квартиры сняты с растрового плана заказчика с частичными размерами (рисунок не в масштабе): помещения выровнены по подписанным размерам мебели и проходов.

К-2 — Высота потолка на плане заказчика не указана, принята 2700 мм.

К-4 — Разрешённая мощность квартиры по ТУ неизвестна, принята 15 кВт.

К-5 — Перепланировка (гардеробная-постирочная при спальне, Г-образный коридор, широкий проём прихожая гостиная, гостевой санузел у прихожей): несущие…

К-6 — Климатический подрайон (СП 131.13330) не задан: принят не северный — жилые комнаты и кухня под потолком от 2,5 м (СП 54, п. 5.12).

К-7 — Проёмы скрытых дверей Д-2 … Д-7 по плану заказчика высотой 2100 мм, полотно расчётное 2000 мм (ряд UNION FILO-60 Piatto).

К-8 — Входная дверь Д-1 (проём 1000 × 2100 мм по плану заказчика): стальной дверной блок не выбран — размер блока и монтажный зазор (ГОСТ 31173-2016) из проёма не выводятся, на…

К-10 — Душ С_07 с трапом (пом. 9, санузел гостевой, по плану заказчика — «душ с трапом и стеклянной перегородкой»): в стяжке 35 мм с облицовкой 14 мм трап не встаёт — монтажная высота…

К-11 — Ванна С_01 отдельностоящая со смесителем напольным (пом. 7, ванная, по заказчику): подвод ХВ и ГВ к стойке и выпуск Ø50 идут из пола, а стяжка ванной 35 мм их не укрывает — под…

К-12 — Проверяющий («Пров.») и нормоконтролёр («Н. контр.») комплекта не назначены: графы штампа пусты на всех листах, данные проекта и данные проекта не заданы.

К-17 — Циркуляция ГВС в данных не задана — циркуляционного трубопровода на схеме нет.

К-19 — Кухня-гостиная (пом. 4, 45,5 м², два окна): мощность приборов не подтверждена расчётом — РО-5 500×600 (вынесен из модулей, ИЗ-6) и низкий РО-6 1400×200 под банкеткой-экраном…

К-20 — ТВ-стена M_24: низ ниши ТВ (+900) — в 150 мм над верхом ниши биокамина (+750).



| | | | | | | | | |
|---|---|---|---|---|---|---|---|---|
| | | | | | Проект: Квартира с кабинетом | | | |
| | Лист | № док. | Подпись | Дата | Ваш проект на одной странице | Стадия | Лист | Листов |
| Дизайнер | Кырлан А.С. | | | 04.11.26 | | П | 3 | 127 |



| | | | | | | |
|---|---|---|---|---|---|---|
| | | | | | Проект: Квартира с кабинетом | |
| | Лист | № док. | Подпись | Дата | Визуализация спальни | Стадия / Лист / Листов |
| Дизайнер | Кырлан А.С. | | | 04.11.26 | | П / 4 / 127 |

выпуск 04.11.2026 № 627e1ac6ce · стр. 4 из 127



| | | | | | |
|---|---|---|---|---|---|
| | | | | | Проект: Квартира с кабинетом |
| | Лист | № док. | Подпись | Дата | |
| Дизайнер | Кырлан А.С. | | | 04.11.26 | Визуализация спальни |
| | | | | | |

| Стадия | Лист | Листов |
|---|---|---|
| П | 5 | 127 |



| | | | | | | | | |
|---|---|---|---|---|---|---|---|---|
| | | | | | Проект: Квартира с кабинетом | | | |
| | Лист | № док. | Подпись | Дата | Визуализация спальни | Стадия | Лист | Листов |
| Дизайнер | Кырлан А.С. | | | 04.11.26 | | П | 6 | 127 |



| | | | | | |
|---|---|---|---|---|---|
| | | | | | Проект: Квартира с кабинетом |
| | Лист | № док. | Подпись | Дата | Визуализация: Гардеробная-постирочная |
| Дизайнер | Кырлан А.С. | | | 04.11.26 | |

| Стадия | Лист | Листов |
|---|---|---|
| П | 7 | 127 |



| | | | | | | |
|---|---|---|---|---|---|---|
| | | | | | Проект: Квартира с кабинетом | |
| | Лист | № док. | Подпись | Дата | Визуализация кабинета | Стадия / Лист / Листов |
| Дизайнер | Кырлан А.С. | | | 04.11.26 | | П / 8 / 127 |



| | | | | | |
|---|---|---|---|---|---|
| | | | | | Проект: Квартира с кабинетом |
| | Лист | № док. | Подпись | Дата | |
| Дизайнер | Кырлан А.С. | | | 04.11.26 | Визуализация кабинета |
| | | | | | |

| Стадия | Лист | Листов |
|---|---|---|
| П | 9 | 127 |



| | | | | | Проект: Квартира с кабинетом | | | |
|---|---|---|---|---|---|---|---|---|
| | Лист | № док. | Подпись | Дата | Визуализация кабинета | Стадия | Лист | Листов |
| Дизайнер | Кырлан А.С. | | | 04.11.26 | | П | 10 | 127 |



| | | | | | | |
|---|---|---|---|---|---|---|
| | | | | | Проект: Квартира с кабинетом | |
| | Лист | № док. | Подпись | Дата | Визуализация кухни-гостиной | Стадия / Лист / Листов |
| Дизайнер | Кырлан А.С. | | | 04.11.26 | | П / 11 / 127 |



| | | | | | | |
|---|---|---|---|---|---|---|
| | | | | | Проект: Квартира с кабинетом | |
| | Лист | № док. | Подпись | Дата | Визуализация кухни-гостиной | Стадия / Лист / Листов |
| Дизайнер | Кырлан А.С. | | | 04.11.26 | | П / 12 / 127 |

выпуск 04.11.2026 № 627e1ac6ce · стр. 12 из 127




| | | | | | | |
|---|---|---|---|---|---|---|
| | | | | | Проект: Квартира с кабинетом | |
| | Лист | № док. | Подпись | Дата | Визуализация кухни-гостиной | Стадия / Лист / Листов |
| Дизайнер | Кырлан А.С. | | | 04.11.26 | | П / 13 / 127 |

выпуск 04.11.2026 № 627e1ac6ce · стр. 13 из 127



| | | | | | | | | |
|---|---|---|---|---|---|---|---|---|
| | | | | | Проект: Квартира с кабинетом | | | |
| | Лист | № док. | Подпись | Дата | Визуализация кухни-гостиной | Стадия | Лист | Листов |
| Дизайнер | Кырлан А.С. | | | 04.11.26 | | П | 14 | 127 |

выпуск 04.11.2026 № 627e1ac6ce · стр. 14 из 127

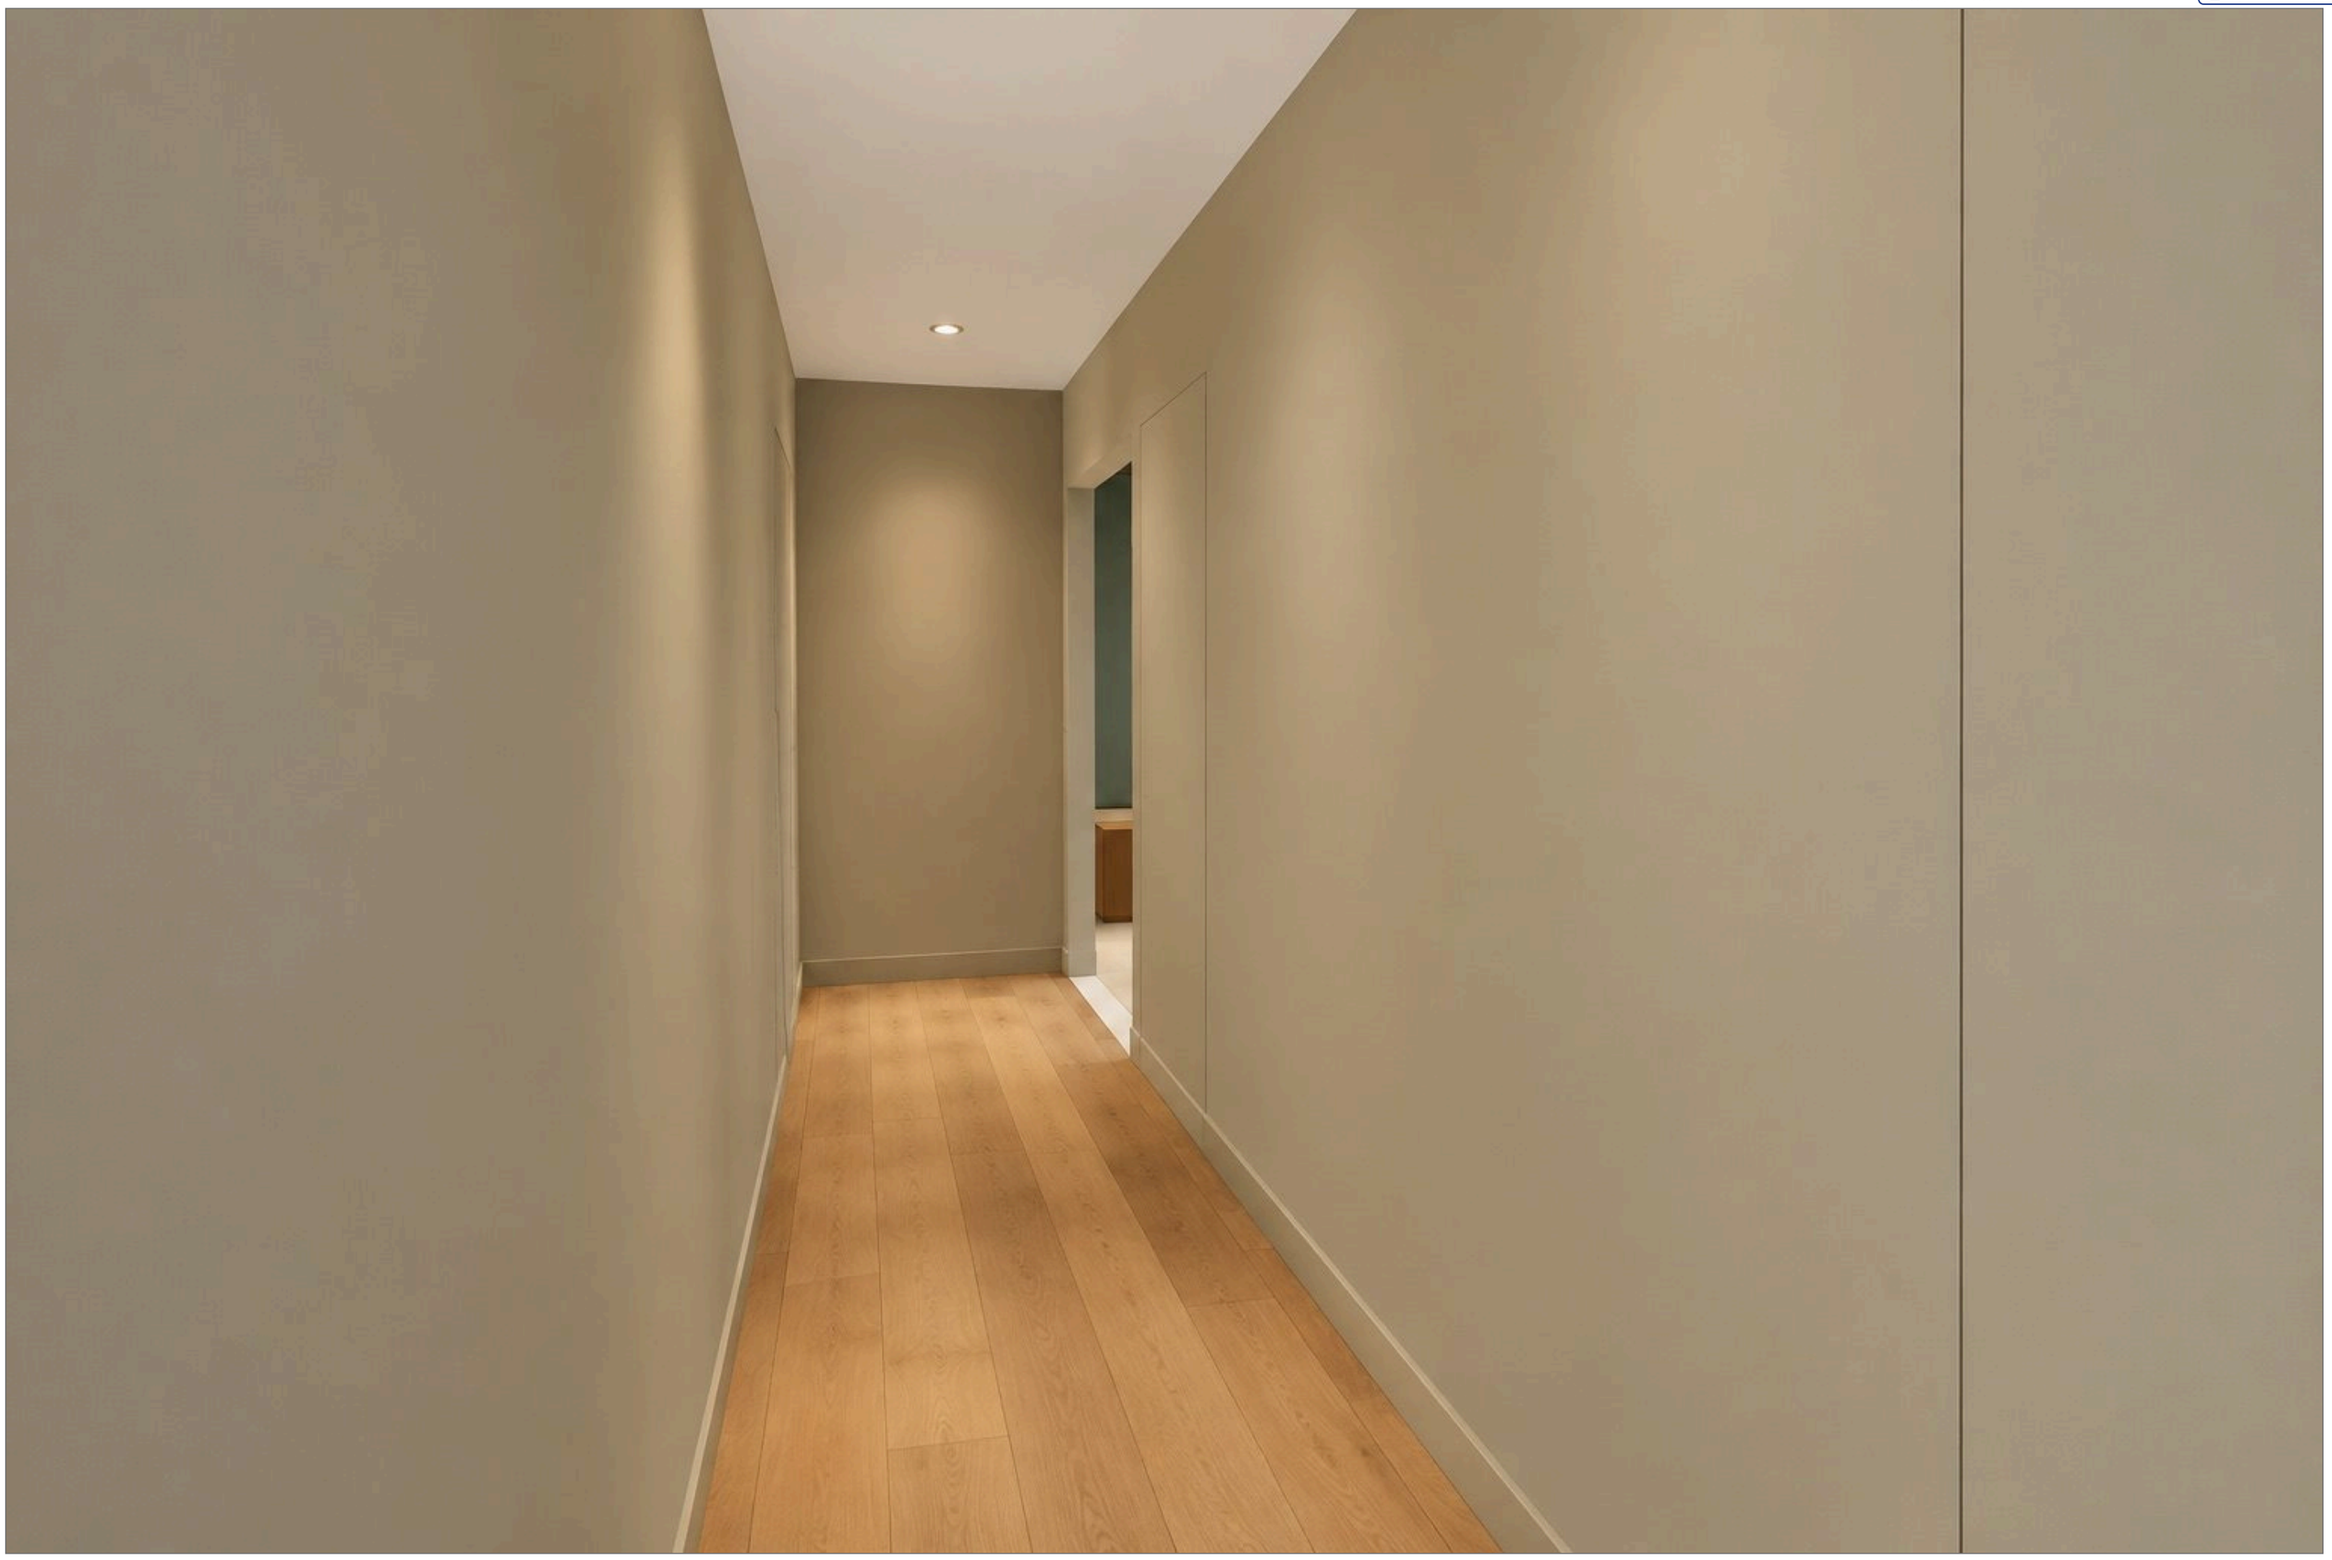

| | | | | | | |
|---|---|---|---|---|---|---|
| | | | | | Проект: Квартира с кабинетом | |
| | Лист | № док. | Подпись | Дата | | |
| Дизайнер | Кырлан А.С. | | | 04.11.26 | Визуализация коридора | Стадия / Лист / Листов |
| | | | | | | П / 15 / 127 |



| | | | | | | |
|---|---|---|---|---|---|---|
| | | | | | Проект: Квартира с кабинетом | |
| | Лист | № док. | Подпись | Дата | Визуализация детской | Стадия / Лист / Листов |
| Дизайнер | Кырлан А.С. | | | 04.11.26 | | П / 16 / 127 |

выпуск 04.11.2026 № 627e1ac6ce · стр. 16 из 127



| | | | | | |
|---|---|---|---|---|---|
| | | | | | Проект: Квартира с кабинетом |
| | Лист | № док. | Подпись | Дата | |
| Дизайнер | Кырлан А.С. | | | 04.11.26 | Визуализация детской |

| Стадия | Лист | Листов |
|---|---|---|
| П | 17 | 127 |



| | | | | | | | |
|---|---|---|---|---|---|---|---|
| | | | | | Проект: Квартира с кабинетом | | |
| | Лист | № док. | Подпись | Дата | Визуализация детской | Стадия | Лист | Листов |
| Дизайнер | Кырлан А.С. | | | 04.11.26 | | П | 18 | 127 |



| | | | | | | |
|---|---|---|---|---|---|---|
| | | | | | Проект: Квартира с кабинетом | |
| | Лист | № док. | Подпись | Дата | Визуализация ванной | Стадия / Лист / Листов |
| Дизайнер | Кырлан А.С. | | | 04.11.26 | | П / 19 / 127 |



| | | | | | | | | |
|---|---|---|---|---|---|---|---|---|
| | | | | | Проект: Квартира с кабинетом | | | |
| | Лист | № док. | Подпись | Дата | Визуализация ванной | Стадия | Лист | Листов |
| Дизайнер | Кырлан А.С. | | | 04.11.26 | | П | 20 | 127 |

выпуск 04.11.2026 № 627e1ac6ce · стр. 20 из 127



| | | | | | | |
|---|---|---|---|---|---|---|
| | | | | | Проект: Квартира с кабинетом | |
| | Лист | № док. | Подпись | Дата | Визуализация ванной | Стадия / Лист / Листов |
| Дизайнер | Кырлан А.С. | | | 04.11.26 | | П / 21 / 127 |



| | | | | | | |
|---|---|---|---|---|---|---|
| | | | | | Проект: Квартира с кабинетом | |
| | Лист | № док. | Подпись | Дата | Визуализация прихожей | Стадия / Лист / Листов |
| Дизайнер | Кырлан А.С. | | | 04.11.26 | | П / 22 / 127 |



| | | | | | | |
|---|---|---|---|---|---|---|
| | | | | | Проект: Квартира с кабинетом | |
| | Лист | № док. | Подпись | Дата | Визуализация прихожей | Стадия / Лист / Листов |
| Дизайнер | Кырлан А.С. | | | 04.11.26 | | П / 23 / 127 |



| | | | | | | |
|---|---|---|---|---|---|---|
| | | | | | Проект: Квартира с кабинетом | |
| | Лист | № док. | Подпись | Дата | Визуализация прихожей | Стадия / Лист / Листов |
| Дизайнер | Кырлан А.С. | | | 04.11.26 | | П / 24 / 127 |



| | | | | | |
|---|---|---|---|---|---|
| | | | | | Проект: Квартира с кабинетом |
| | Лист | № док. | Подпись | Дата | |
| Дизайнер | Кырлан А.С. | | | 04.11.26 | Визуализация: Санузел гостевой |

| Стадия | Лист | Листов |
|---|---|---|
| П | 25 | 127 |



| | | | | | | | | |
|---|---|---|---|---|---|---|---|---|
| | | | | | Проект: Квартира с кабинетом | | | |
| | Лист | № док. | Подпись | Дата | Визуализация: Санузел гостевой | Стадия | Лист | Листов |
| Дизайнер | Кырлан А.С. | | | 04.11.26 | | П | 26 | 127 |

## Список листов


| Лист | Наименование |
|---|---|
| 1 | Титульный лист |
| 2 | Визуализация. Вид сверху |
| 3 | Ваш проект на одной странице |
| 4 | Визуализация спальни |
| 5 | Визуализация спальни |
| 6 | Визуализация спальни |
| 7 | Визуализация: Гардеробная-постирочная |
| 8 | Визуализация кабинета |
| 9 | Визуализация кабинета |
| 10 | Визуализация кабинета |
| 11 | Визуализация кухни-гостиной |
| 12 | Визуализация кухни-гостиной |
| 13 | Визуализация кухни-гостиной |
| 14 | Визуализация кухни-гостиной |
| 15 | Визуализация коридора |
| 16 | Визуализация детской |
| 17 | Визуализация детской |
| 18 | Визуализация детской |
| 19 | Визуализация ванной |
| 20 | Визуализация ванной |
| 21 | Визуализация ванной |
| 22 | Визуализация прихожей |
| 23 | Визуализация прихожей |
| 24 | Визуализация прихожей |
| 25 | Визуализация: Санузел гостевой |
| 26 | Визуализация: Санузел гостевой |
| 27 | Список листов |
| 28 | Список листов |
| 29 | Как читать альбом |
| 30 | План планировки от заказчика |
| 31 | План монтажный |
| 32 | Кухня (пом. 4). Монтажная схема |
| 33 | Шкафы. Монтажная схема. Лист 1 из 2 |
| 34 | Шкафы. Монтажная схема. Лист 2 из 2 |
| 35 | Карта покрытий стен |
| 36 | Колерная карта |
| 37 | План размещения мебели и оборудования |
| 38 | Спецификация мебели и оборудования |
| 39 | Спецификация мебели и оборудования (продолжение) |
| 40 | Спецификация мебели и оборудования (продолжение) |
| 41 | Ведомости изделий, техники и фурнитуры |
| 42 | План выводов сантехники |
| 43 | Схема разводки водопровода и канализации |
| 44 | Аксонометрическая схема В1 (холодное водоснабжение) |
| 45 | Аксонометрическая схема Т3 (горячее водоснабжение) |
| 46 | Аксонометрическая схема К1 (канализация) |
| 47 | Развёртки мокрых зон: выводы ВК. Кухня-гостиная |
| 48 | Развёртки мокрых зон: выводы ВК. Ванная (лист 1 из 2) |
| 49 | Развёртки мокрых зон: выводы ВК. Ванная (лист 2 из 2) |
| 50 | Развёртки мокрых зон: выводы ВК. Санузел гостевой (лист 1 из 2) |
| 51 | Развёртки мокрых зон: выводы ВК. Санузел гостевой (лист 2 из 2) |
| 52 | Спецификация сантехнического оборудования |
| 53 | Раскладка плитки. Ванная. Развёртки стен |
| 54 | Раскладка плитки. Санузел гостевой. Развёртки стен |
| 55 | План размещения дверей |
| 56 | Ведомость заполнения проёмов |
| 57 | План потолков |
| 58 | Разрезы и узлы потолков |
| 59 | Разрезы и узлы потолков (продолжение) |
| 60 | Разрезы и узлы потолков (продолжение) |
| 61 | Сечения потолков М 1:10 |
| 62 | Сечения потолков М 1:10 |
| 63 | Однолинейная схема щита |
| 64 | Однолинейная схема щита (продолжение) |


| | | | | | |
|---|---|---|---|---|---|
| | | | | | Проект: Квартира с кабинетом |
| | Лист | № док. | Подпись | Дата | Список листов |
| Дизайнер | Кырлан А.С. | | | 04.11.26 | Стадия: П; Лист: 27; Листов: 127 |

## Список листов (продолжение)


| Лист | Наименование |
|---|---|
| 65 | План розеток и электровыводов |
| 66 | План слаботочных сетей |
| 67 | План освещения |
| 68 | Техническое задание на подбор светильников |
| 69 | Управление светильниками |
| 70 | План вентиляции |
| 71 | План отопления |
| 72 | План покрытий пола |
| 73 | Раскладка плитки. Планы полов |
| 74 | Раскладка плитки. Прихожая. Фартук кухни |
| 75 | Развёртка стены А. Спальня (пом. 1) |
| 76 | Развёртка стены Б. Спальня (пом. 1) |
| 77 | Привязки электроточек, стена Б. Спальня (пом. 1) |
| 78 | Развёртка стены В. Спальня (пом. 1) |
| 79 | Развёртка стены Г. Спальня (пом. 1) |
| 80 | Развёртки стен А, Б. Гардеробная-постирочная (пом. 2) |
| 81 | Развёртки стен В, Г. Гардеробная-постирочная (пом. 2) |
| 82 | Развёртка стены А. Кабинет (пом. 3) |
| 83 | Развёртка стены Б. Кабинет (пом. 3) |
| 84 | Развёртка стены В. Кабинет (пом. 3) |
| 85 | Развёртка стены Г. Кабинет (пом. 3) |
| 86 | Развёртка стены Г. Кухня-гостиная (пом. 4), кухонный фронт |
| 87 | Привязки электроточек, стена Г. Кухня-гостиная (пом. 4) |
| 88 | Развёртка стены А. Кухня-гостиная (пом. 4), кухонный фронт |
| 89 | Привязки электроточек и выводов ВК, стена А. Кухня-гостиная (пом. 4) |
| 90 | Развёртка стены Б. Кухня-гостиная (пом. 4) |
| 91 | Привязки электроточек, стена Б. Кухня-гостиная (пом. 4) |
| 92 | Развёртка стены В. Кухня-гостиная (пом. 4) |
| 93 | Развёртки стен А1, Г. Коридор (пом. 5) |
| 94 | Развёртка стены А2. Коридор (пом. 5) |
| 95 | Развёртка стены В. Коридор (пом. 5) |
| 96 | Развёртка стены А. Детская (пом. 6) |
| 97 | Развёртка стены Б. Детская (пом. 6) |
| 98 | Привязки электроточек, стена Б. Детская (пом. 6) |
| 99 | Развёртка стены В. Детская (пом. 6) |
| 100 | Развёртка стены Г. Детская (пом. 6) |
| 101 | Развёртки стен А, Б. Ванная (пом. 7) |
| 102 | Развёртки стен В, Г. Ванная (пом. 7) |
| 103 | Привязки электроточек и выводов ВК, стены Б, Г. Ванная (пом. 7) |
| 104 | Развёртки стен Б, В. Прихожая (пом. 8) |
| 105 | Развёртка стены Г. Прихожая (пом. 8) |
| 106 | Развёртки стен А, Б. Санузел гостевой (пом. 9) |
| 107 | Привязки электроточек и выводов ВК, стена А. Санузел гостевой (пом. 9) |
| 108 | Развёртки стен В, Г. Санузел гостевой (пом. 9) |
| 109 | Открытые вопросы, принятые допущения и конфликты. Лист 1 из 3 |
| 110 | Открытые вопросы, принятые допущения и конфликты. Лист 2 из 3 |
| 111 | Открытые вопросы, принятые допущения и конфликты. Лист 3 из 3 |
| Д_1 | Система хранения M_06 |
| Д_2 | Система хранения M_07 |
| Д_3 | Шкаф распашной M_08 |
| Д_4 | ТВ-стена M_24 |
| Д_5 | Шкаф распашной M_25 |
| Д_6 | Шкаф распашной M_26 |
| Д_7 | Тумба под раковину M_29 |
| Д_8 | Шкаф-купе M_30 |
| Д_9 | Кухня (пом. 4). Развёртка гарнитура |
| Д_10 | Остров M_19 (пом. 4). Чертёж изделия |
| С1 | Ведомость отделки помещений. Лист 1 из 2 |
| С2 | Ведомость отделки помещений. Лист 2 из 2 |
| С3 | Спецификация отделочных материалов |
| С4 | Список покупок |
| С5 | Список покупок (окончание) |
| С6 | Узлы |


## Общие указания

1. Размеры даны в мм от чистовых поверхностей стен: слой штукатурки 20 мм по блоку и 5 мм шпаклёвки по ГКЛ учтён. Перед заказом встроенной мебели — контрольный обмер после штукатурки.
2. Привязки мебели — от стен и углов помещения, а не от другой мебели.
3. Розетки, выводы и выключатели под мебель — см. лист 65 «План розеток и электровыводов»; сантехприборы и выводы воды — лист 42.
4. План расстановки не является документацией для изготовления мебели: изделия — по чертежам мебельщика; покупную мебель заменять только на изделия не больше габарита из спецификации (лист 38).
5. Встроенная мебель «стена в стену» — с зазором 10 мм с каждой стороны или с компенсаторами.
6. Развёртки — вид на стену изнутри помещения, по часовой стрелке; расположение стен на схеме листа развёртки; размеры — в мм по чистовым поверхностям; отметки — в м от ±0,000; высоты H — от чистого пола помещения до оси изделия, у декора — до центра.
7. Красная цепочка — привязки электроточек и выводов по осям от угла чистовых стен; высота H — у знака, от чистого пола до оси; высоты мебели, проёмов и границ отделки колонкой отметок слева. Стена с 5 и более точками или с мелкими звеньями привязок показана двумя видами: архитектурная развёртка (мебель, отделка, проёмы, высоты) и вид «Привязки» на отдельном листе — точки и выводы с марками, одна цепочка по осям и таблица привязок (каждая точка — строка).
8. У знака электроточки: марка (Р — розетка, S — выключатель, Св — светильник, ЭВ вывод кабеля), ×N — число постов в рамке, гр. — группа щита, H — высота оси от чистого пола, мм; группы по клавишам выключателя — на листе выключателей.
9. Схема мебели, приборов и декора не является технической документацией для производства мебели; габариты — по паспортам изделий.
10. Марки позиций: M_NN — мебель, ОБ_NN — оборудование, С_NN — сантехника; О-N отделка (ведомость отделочных материалов, серия С).
11. Размеры мебели и изделий на заказ уточнить по месту после отделочных работ.

| | | | | | |
|---|---|---|---|---|---|
| | | | | | Проект: Квартира с кабинетом |
| | Лист | № док. | Подпись | Дата | Список листов |
| Дизайнер | Кырлан А.С. | | | 04.11.26 | |

| Стадия | Лист | Листов |
|---|---|---|
| П | 28 | 127 |

## Что в альбоме

Альбом — дизайн-проект с рабочими чертежами для ремонта. Листы идут в порядке работ: титул и вводные, реестр открытых вопросов и решений, планы (обмер, монтаж стен, мебель, двери, потолки, полы), инженерия (сантехника, электрика, вентиляция и отопление), развёртки стен с визуализациями помещений, чертежи мебели, ведомости материалов и узлы.

Вам как заказчику — титул, эта вводная, «Ваш проект на одной странице», реестр вопросов, план мебели, визуализации и развёртки, ведомости мебели и материалов. Подрядчику — всё остальное: монтажные планы, привязки выводов и розеток, узлы, ведомости объёмов.

## Знаки на листах

Без знака — решение утверждено или подтверждено обмером.

## Что проверить до ремонта

1. Розетки у кровати и рабочего места: хватает ли их с каждой стороны кровати и над столом (план розеток — лист 65).

2. Выводы под технику — варочная панель, духовка, посудомойка, стиральная машина, бойлер: совпадают ли с выбранными моделями (листы 38, 39, 40, 65).

3. Высоты розеток, выключателей и выводов даны от чистого пола: если мебель или техника будут другими — скажите до штробления стен.

## Номера записей

К-N — открытый вопрос: чего не хватает или что выбрать (варианты и рекомендация — в тексте). Пока ответа нет, действует строка «если решения нет».

Кф-N — конфликт между разделами (например, мебель и радиатор в одном месте); закрывается решением, которое записывается как ИЗ-N.

ИЗ-N — изменение проекта: что было, что стало и кто утвердил. Изменение без подписи предложение.

Все записи — на листе реестра сразу после вводных; на других листах на них стоят ссылки.

## Почему альбом предварительный

Обмера на объекте не было: размеры взяты с плана заказчика. Технические условия (мощность, вода, вентиляция дома) не получены, часть решений ждёт вашего ответа. Пока в реестре есть открытые вопросы, альбом предварительный — пометка в штампе снимается закрытием вопросов, а не стиранием.

Правку к любому листу можно оставить по кнопке «Правка к листу» или на сайте студии: дизайн-студия-квартир.рф — укажите номер листа и что изменить.

3 круга правок входят в цену; условия — в договоре и на странице вашего заказа на сайте студии.


Шифр проекта ГД-2026-008-АИ

| | | | | | |
|---|---|---|---|---|---|
| | | | | | Проект: Квартира с кабинетом |
| | Лист | № док. | Подпись | Дата | |
| Дизайнер | Кырлан А.С. | | | 04.11.26 | Как читать альбом |
| | | | | | Стадия: П; Лист: 29; Листов: 127 |

выпуск 04.11.2026 № 627e1ac6ce · стр. 29 из 127

## Отметки по высоте

**±0,000** чистый пол пом. 1–6, 8; отсчёт высот
**−0,015** чистый пол пом. 7, 9, ниже на 15 мм
**−0,064** верх плиты — расчёт, не замер (задание на обмер)
**сущ. пол** снимается до плиты; не замерен (задание на обмер)

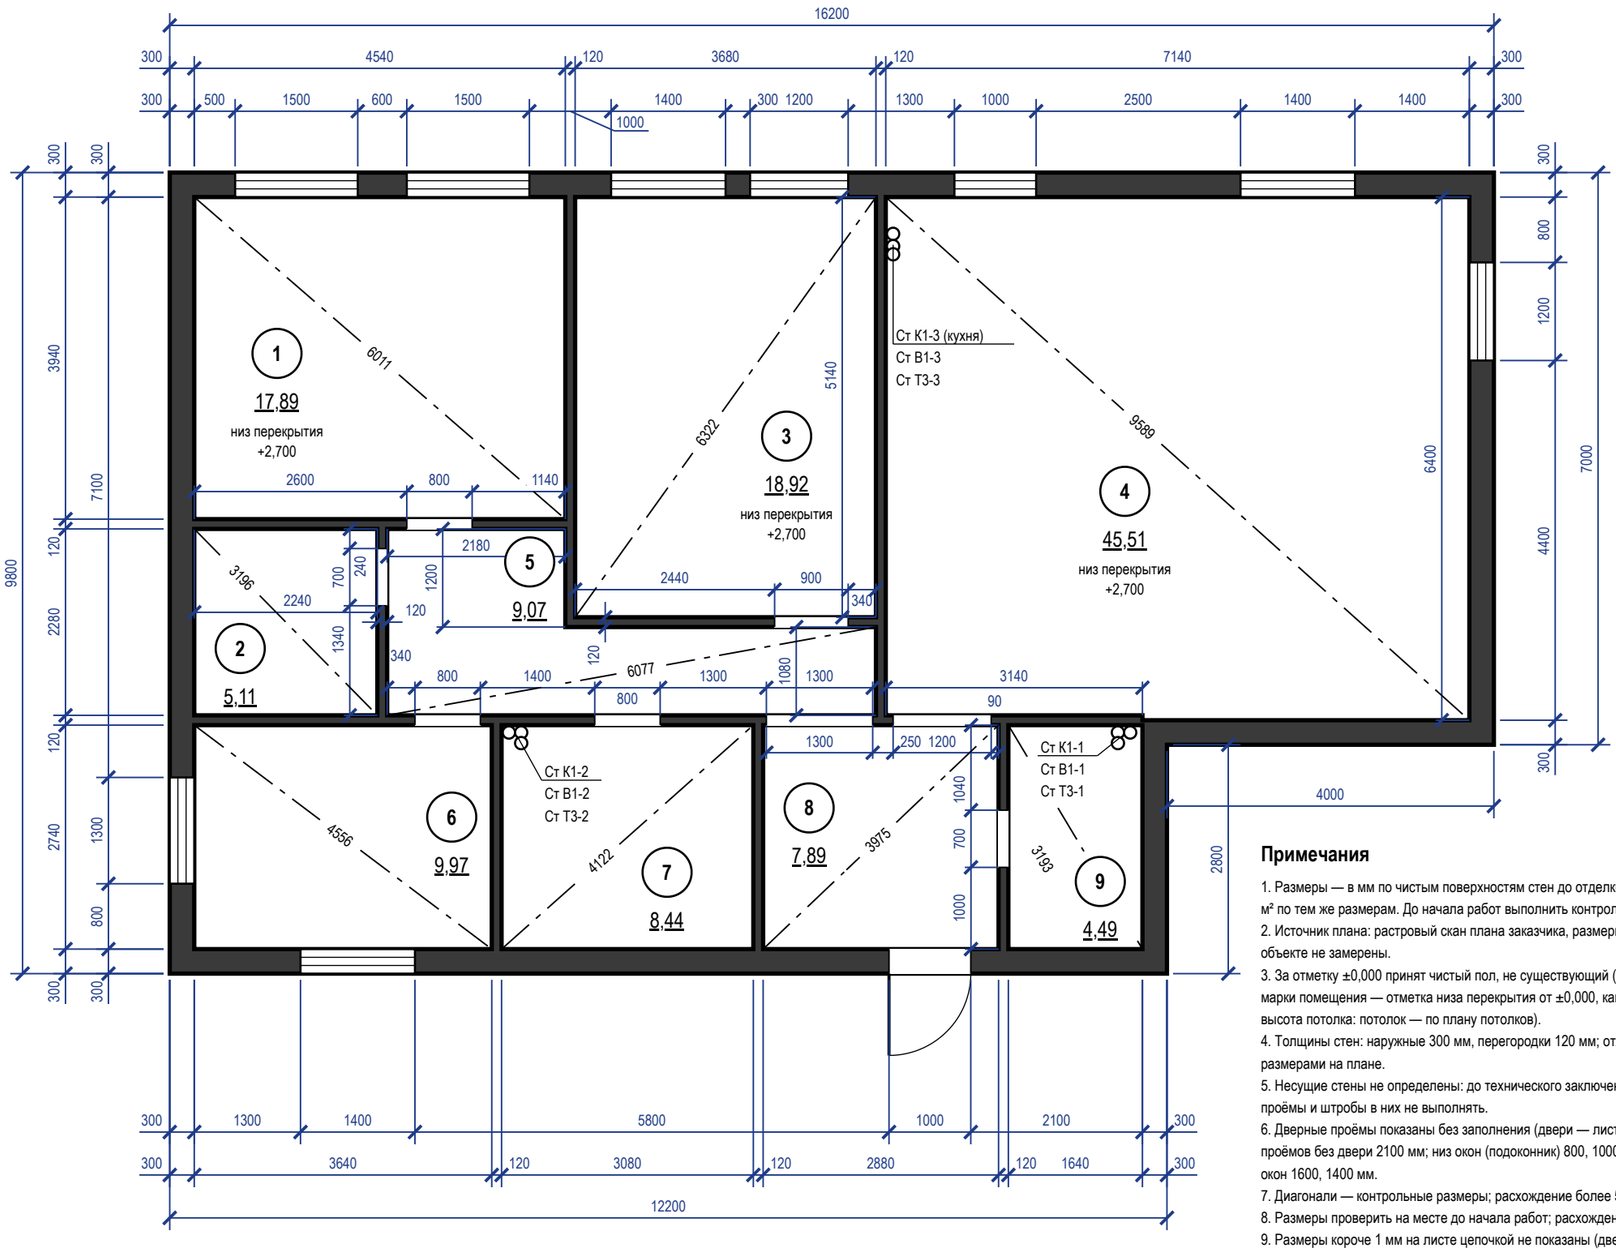


## Экспликация помещений

| № | Наименование | Площадь, м² |
|---|---|---|
| 1 | Спальня | 17,89 |
| 2 | Гардеробная-постирочная | 5,11 |
| 3 | Кабинет | 18,92 |
| 4 | Кухня-гостиная | 45,51 |
| 5 | Коридор | 9,07 |
| 6 | Детская | 9,97 |
| 7 | Ванная | 8,44 |
| 8 | Прихожая | 7,89 |
| 9 | Санузел гостевой | 4,49 |
| | **Итого (общая площадь)** | **127,29** |

## Условные обозначения


- существующие стены (сечение)
- окно (рама, остекление)
- проём существующий, без заполнения (откосы)
- стояк: К1 — канализация, В1 — ХВС, Т3 — ГВС
- диагональ помещения — контроль прямоугольности
- (1) номер помещения, площадь м²

## Примечания

1. Размеры — в мм по чистым поверхностям стен до отделки (по плану заказчика); площади — в м² по тем же размерам. До начала работ выполнить контрольный обмер.
2. Источник плана: растровый скан плана заказчика, размеры сняты с размерных цепочек, на объекте не замерены.
3. За отметку ±0,000 принят чистый пол, не существующий (блок отметок). «Низ перекрытия» у марки помещения — отметка низа перекрытия от ±0,000, как на развёртках и плане потолков (не высота потолка: потолок — по плану потолков).
4. Толщины стен: наружные 300 мм, перегородки 120 мм; отличающиеся толщины и уступы размерами на плане.
5. Несущие стены не определены: до технического заключения все стены считать несущими; проёмы и штробы в них не выполнять.
6. Дверные проёмы показаны без заполнения (двери — лист 56); высота дверных проёмов 2100 мм, проёмов без двери 2100 мм; низ окон (подоконник) 800, 1000, 900 мм от чистого пола, высота окон 1600, 1400 мм.
7. Диагонали — контрольные размеры; расхождение более 5 мм подписать на плане как перекос.
8. Размеры проверить на месте до начала работ; расхождение контрольных промеров ≤ 2 %.
9. Размеры короче 1 мм на листе цепочкой не показаны (две выносные линии на таком расстоянии сливаются): пом. 5, стена В — 40 мм от проёма до угла; пом. 8, стена А — 40 мм от угла до проёма.

| | | | | | | |
|---|---|---|---|---|---|---|
| | | | | | Проект: Квартира с кабинетом | **М 1:75** |
| | Лист | № док. | Подпись | Дата | План планировки от заказчика | Стадия / Лист / Листов |
| Дизайнер | Кырлан А.С. | | | 04.11.26 | | П / 30 / 127 |

выпуск 04.11.2026 № 627e1ac6ce · стр. 30 из 127

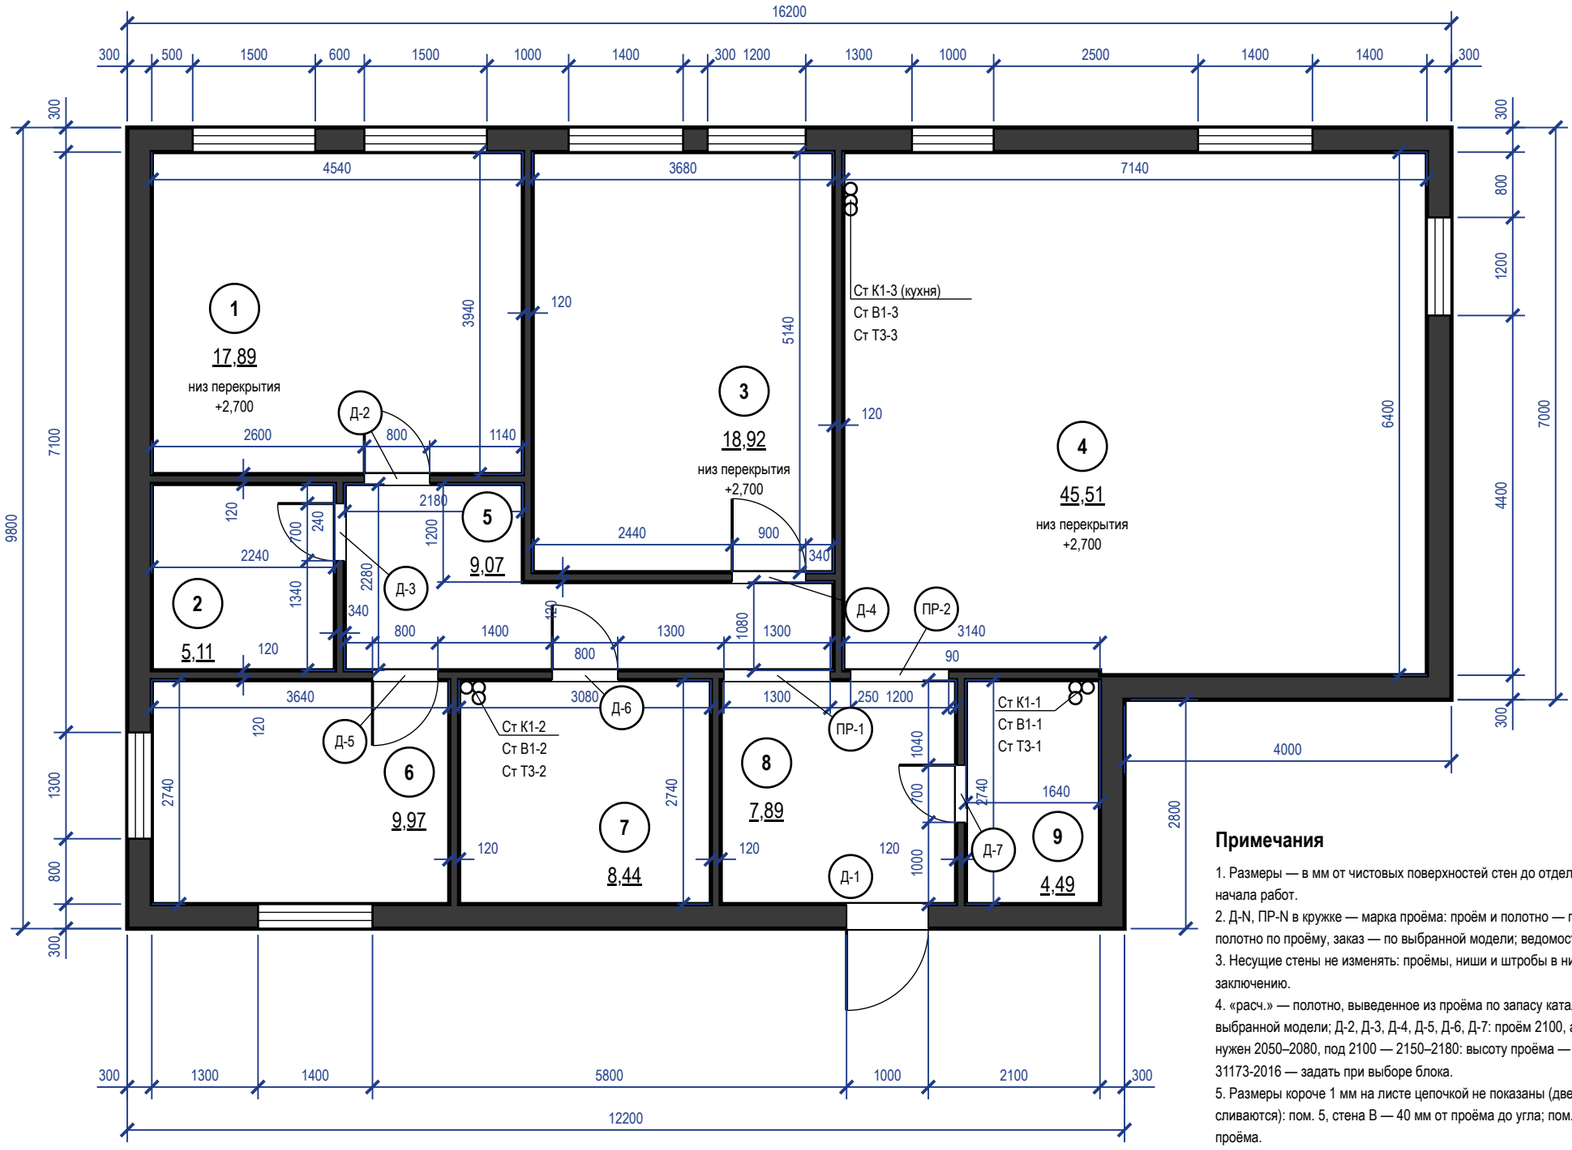


## Экспликация помещений

| № | Наименование | Площадь, м² |
|---|---|---|
| 1 | Спальня | 17,89 |
| 2 | Гардеробная-постирочная | 5,11 |
| 3 | Кабинет | 18,92 |
| 4 | Кухня-гостиная | 45,51 |
| 5 | Коридор | 9,07 |
| 6 | Детская | 9,97 |
| 7 | Ванная | 8,44 |
| 8 | Прихожая | 7,89 |
| 9 | Санузел гостевой | 4,49 |
| | **Итого (общая площадь)** | **127,29** |

## Таблица проёмов


| Марка | Наименование | Проём ш×в, мм | Полотно (расч.) |
|---|---|---|---|
| Д-1 | Дверь входная | 1000×2100 | блок — задать |
| Д-2 | Дверь скрытого монтажа | 800×2100 | 700×2000 |
| Д-3 | Дверь скрытого монтажа | 700×2100 | 600×2000 |
| Д-4 | Дверь скрытого монтажа | 900×2100 | 800×2000 |
| Д-5 | Дверь скрытого монтажа | 800×2100 | 700×2000 |
| Д-6 | Дверь скрытого монтажа | 800×2100 | 700×2000 |
| Д-7 | Дверь скрытого монтажа | 700×2100 | 600×2000 |
| ПР-1 | Проём без заполнения | 1300×2100 | |
| ПР-2 | Проём без заполнения | 1200×2100 | |

## Примечания


1. Размеры — в мм от чистовых поверхностей стен до отделки; размеры уточнить по месту до начала работ.
2. Д-N, ПР-N в кружке — марка проёма: проём и полотно — по таблице проёмов, «расч.» полотно по проёму, заказ — по выбранной модели; ведомость, отделка и фурнитура — лист 56.
3. Несущие стены не изменять: проёмы, ниши и штробы в них — только по техническому заключению.
4. «расч.» — полотно, выведенное из проёма по запасу каталогов; заказ — по таблице проёмов выбранной модели; Д-2, Д-3, Д-4, Д-5, Д-6, Д-7: проём 2100, а под полотно 2000 по каталогам нужен 2050–2080, под 2100 — 2150–2180: высоту проёма — по модели; Д-1: входной блок по ГОСТ 31173-2016 — задать при выборе блока.
5. Размеры короче 1 мм на листе цепочкой не показаны (две выносные линии на таком расстоянии сливаются): пом. 5, стена В — 40 мм от проёма до угла; пом. 8, стена А — 40 мм от угла до проёма.

| | | | | | | |
|---|---|---|---|---|---|---|
| | | | | | Проект: Квартира с кабинетом | М 1:75 |
| | Лист | № док. | Подпись | Дата | План монтажный | Стадия / Лист / Листов |
| Дизайнер | Кырлан А.С. | | | 04.11.26 | | П / 31 / 127 |

## Привязка выводов и крепление модулей

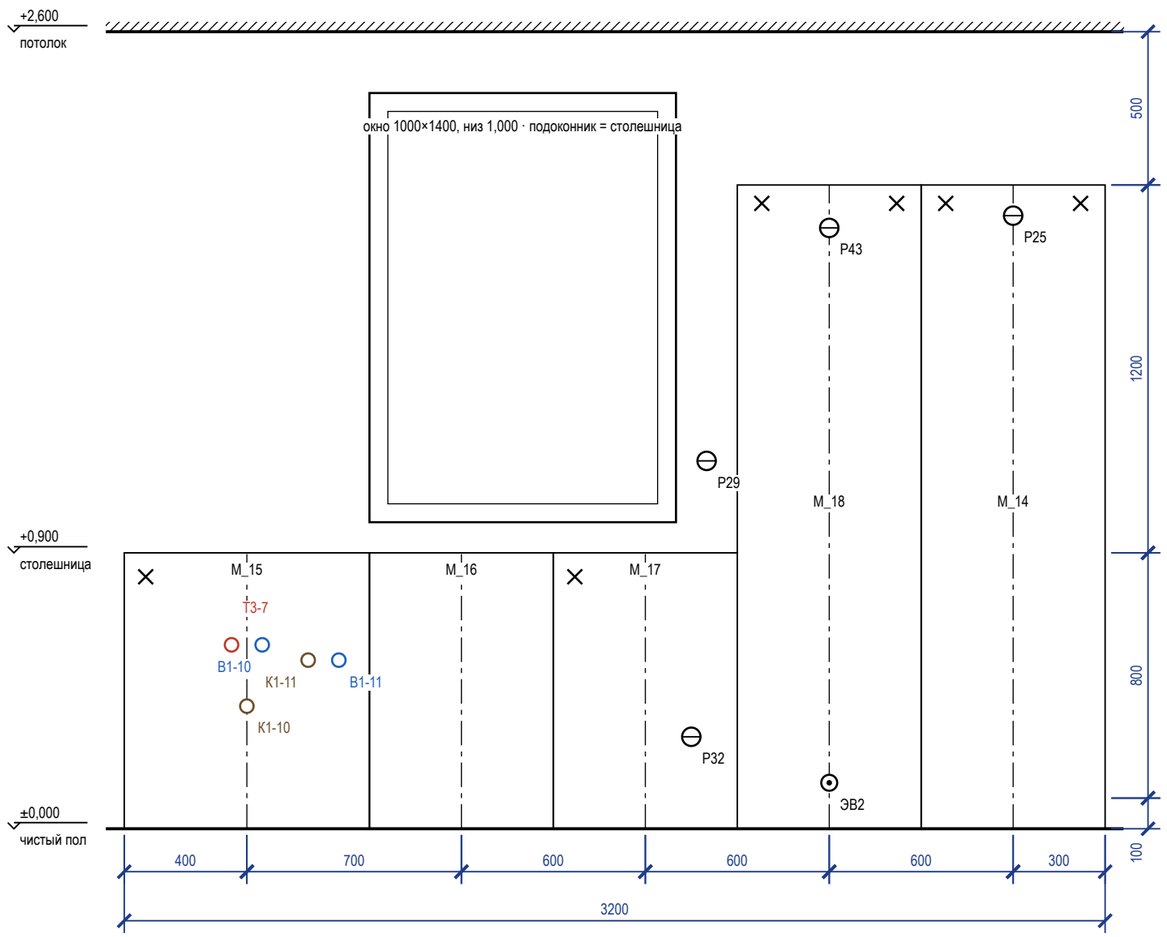


## План столешницы

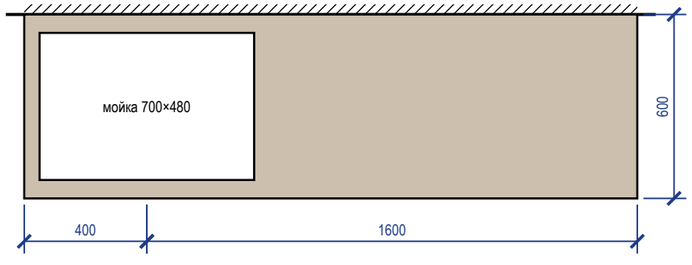


## Привязка выводов к осям модулей

| Код | Назначение | Модуль | От оси, мм | H, мм | Размещение |
|---|---|---|---|---|---|
| T3-7 | T3 — межос. 100 | M_15 | −50 | 600 | в модуле мойки |
| K1-10 | K1 Ø50 — мойка | M_15 | 0 | 400 | в модуле мойки |
| B1-10 | B1 — межос. 100 | M_15 | +50 | 600 | в модуле мойки |
| K1-11 | K1 Ø40 — слив ПММ в шкафу мойки | M_15 | +200 | 550 | в модуле мойки |
| B1-11 | B1 — кран ПММ в шкафу мойки | M_15 | +300 | 550 | в модуле мойки |
| P32 | розетка — посудомоечная машина — в соседнем модуле, за ящиком | M_17 | +150 | 300 | в соседнем модуле, за ящиком |
| P29 | розетка — фартук | M_17 | +200 | 1200 | над столешницей (фартук) |
| ЭВ2 | вывод кабеля — духовой шкаф — в цоколе | M_18 | 0 | 150 | за ящиком под нишей, доступ через ящик |
| P43 | розетка — СВЧ — над нишей, съёмная панель | M_18 | 0 | 1960 | над нишами техники, за съёмной панелью антресоли |
| P25 | розетка — холодильник — над нишей, съёмная панель | M_14 | 0 | 2000 | над нишей холодильника, съёмная панель |

## Зазоры под отделку

| Поверхность | Отделка | Зазор, мм | Учесть |
|---|---|---|---|
| фартук | керамогранит | 10 | от чернового основания до корпуса навесных и столешницы |
| стены | окраска | 5 | под штукатурку и шпаклёвку за пеналом |
| пол | инженерная доска | | цоколь — после укладки пола, опоры ±20 мм |

## Условные обозначения


- нижний модуль, пенал (контур)
- ось модуля (от неё — привязка вывода)
- анкер / уголок крепления к стене
- розетка на стене
- вывод кабеля к технике
- B1 — вывод воды B1 / T3, канализации K1

## Примечания


1. Окно над M_16, M_17: низ проёма на 1000 мм от пола, столешница на 900 мм; примыкание столешницы к откосу и подоконнику — до решения: нужно решение заказчика (створка глухая или поворотно-откидная, поднять подоконник); столешницу у окна не раскраивать до решения.
2. Выводы — по проекту электрики и ВК; привязка по горизонтали — от оси модуля (плюс — вправо по виду), по высоте — от чистого пола до оси вывода.
3. Пенал — уголки к стене 2 шт. сверху; нижние модули — стяжками между собой и уголком к стене; ряд выставить по уровню опорами цоколя.
4. Розетки над столешницей — не ниже 150 мм над ней и не за корпусом техники; розетка за ПММ, духовым шкафом и холодильником — только в соседнем модуле или в зоне цоколя с доступом.
5. Столешница — вырезы по шаблонам выбранных моделей мойки и варочной панели; торцы у стены — герметик, пристеночный плинтус.

| | | | | | |
|---|---|---|---|---|---|
| | | | | | Проект: Квартира с кабинетом — **M 1:20** |
| | Лист | № док. | Подпись | Дата | Кухня (пом. 4). Монтажная схема |
| Дизайнер | Кырлан А.С. | | | 04.11.26 | Стадия: П · Лист: 32 · Листов: 127 |


**Система хранения M_06 (пом. 2)**

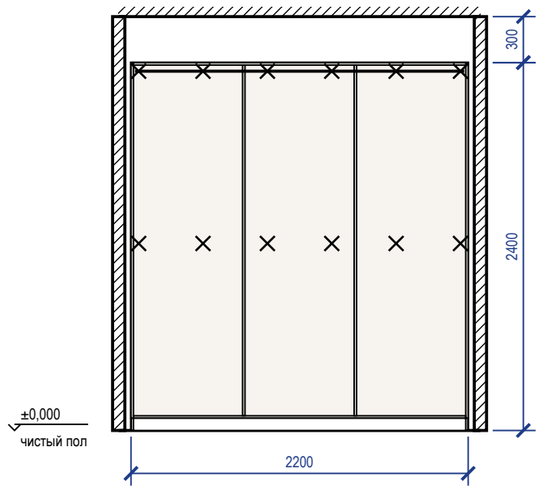



**Система хранения M_07 (пом. 2)**

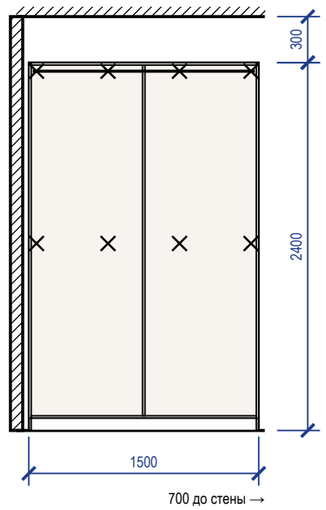


**Шкаф распашной M_08 (пом. 3)**

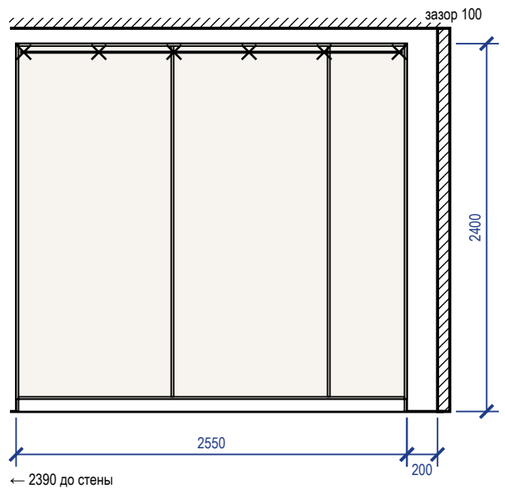


**ТВ-стена M_24 (пом. 4)**

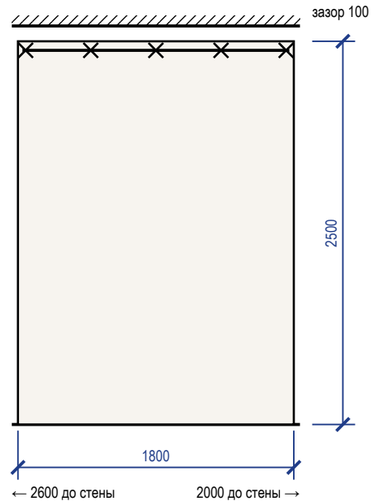


## Крепление и зазоры под отделку (изделия листа 1)

| Марка | Помещение, стена | Основание | Отделка стены | Зазор, мм | Крепёж по планке | От опрокидывания |
|---|---|---|---|---|---|---|
| M_06 | Гардеробная-постирочная (2), стена Г | по основанию — см. таблицу крепежа | окраска | 5 | анкер 12 шт. (2 ряда) | крепление к стене, 3 точки |
| M_07 | Гардеробная-постирочная (2), стена В | по основанию — см. таблицу крепежа | окраска | 5 | анкер 8 шт. (2 ряда) | крепление к стене, 3 точки |
| M_08 | Кабинет (3), стена Г | по основанию — см. таблицу крепежа | окраска | 5 | анкер 6 шт., шаг 490 | уголки 2 шт. |
| M_24 | Кухня-гостиная (4), стена Б | по основанию — см. таблицу крепежа | окраска | 5 | анкер 5 шт., шаг 425 | уголки 2 шт. |

## Крепёж по основанию стены

| Основание стены | Крепёж |
|---|---|
| бетон, ж/б | анкер-шуруп 7,5×72 или дюбель 8×60 с шурупом 5×70 |
| кирпич полнотелый | дюбель 8×80 с шурупом 5×90 |
| газобетон, пазогребень | дюбель для газобетона 10×100 или химический анкер |
| гипсокартон | закладная до обшивки (брус 40×80 или фанера 18 мм), саморез в закладную |

## Условные обозначения


- × — анкер / уголок крепления к стене
- прямоугольник — корпус и полки ЛДСП (вид на стену)
- штриховка — компенсатор — короб до потолка

## Примечания


1. Установочные размеры — от чистого пола и чистых стен; перед установкой контрольный замер после отделки.
2. Порядок: корпус выставить по уровню опорами цоколя → закрепить к стене по задней планке → навесить двери и фасады, отрегулировать зазоры → подогнать и закрепить компенсатор.
3. Анкеры — с шагом не более 500 мм, не ближе 50 мм от края планки; на ГКЛ только в закладную, установленную до обшивки.
4. Скрытые коммуникации под анкеры проверить детектором; трассы электрики по плану розеток.
5. Сборка стоя на месте: M_24 — корпус не собирается лёжа и не поднимается собранным, а собирается в проектном положении у стены; выставление по уровню и крепление к стене выполняются по корпусу, собранному на месте.
6. Монтажная схема на 2 листах, лист 1 из 2; продолжение — на следующем листе схемы. Условные обозначения, таблица крепежа по основанию и примечания повторены на каждом листе.

| | | | | | | |
|---|---|---|---|---|---|---|
| | | | | | Проект: Квартира с кабинетом | **M 1:40** |
| | Лист | № док. | Подпись | Дата | | |
| Дизайнер | Кырлан А.С. | | | 04.11.26 | Шкафы. Монтажная схема. Лист 1 из 2 | Стадия: П; Лист: 33; Листов: 127 |


### Шкаф распашной М_25 (пом. 4)

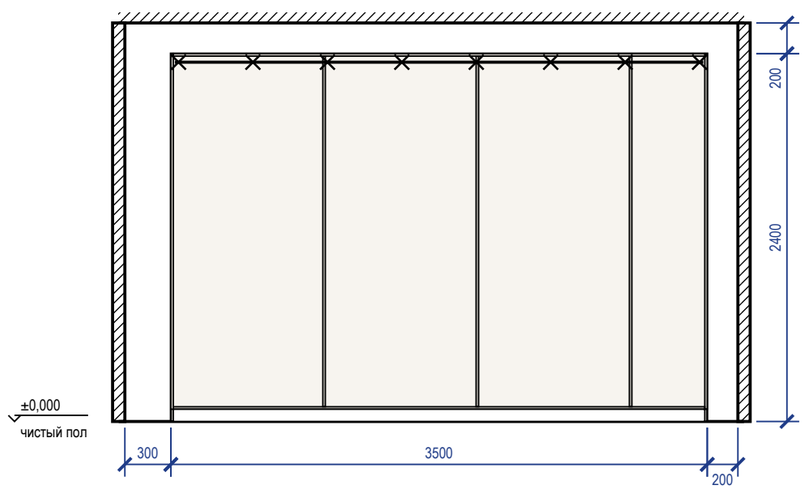



### Шкаф распашной М_26 (пом. 6)

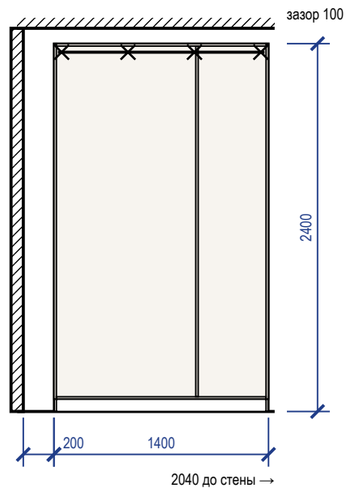


### Тумба под раковину М_29 (пом. 7)

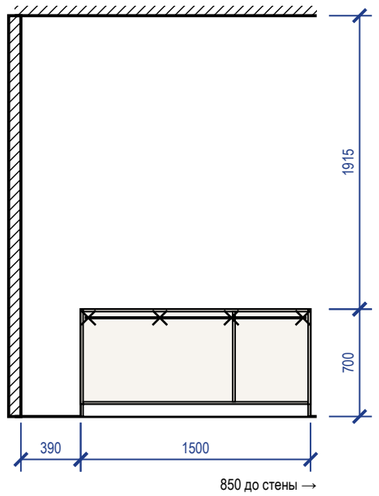


### Шкаф-купе М_30 (пом. 8)

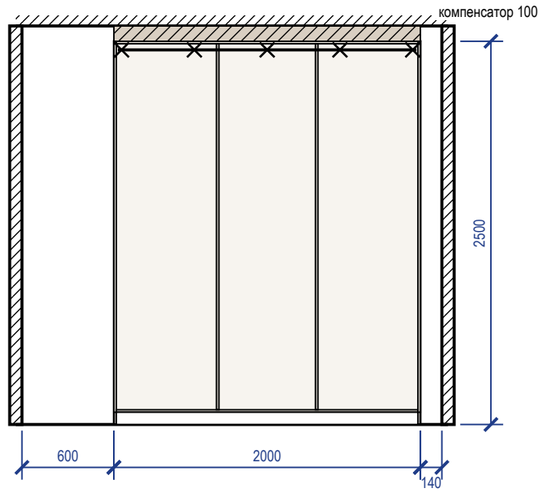


## Крепление и зазоры под отделку (изделия листа 2)

| Марка | Помещение, стена | Основание | Отделка стены | Зазор, мм | Крепёж по планке | От опрокидывания |
|---|---|---|---|---|---|---|
| М_25 | Кухня-гостиная (4), стена В | по основанию — см. таблицу крепежа | окраска | 5 | анкер 8 шт., шаг 486 | уголки 2 шт. |
| М_26 | Детская (6), стена А | по основанию — см. таблицу крепежа | окраска | 5 | анкер 4 шт., шаг 433 | крепление к стене, 2 точки |
| М_29 | Ванная (7), стена Б | по основанию — см. таблицу крепежа | плитка | 10 | анкер 4 шт., шаг 467 | крепление к стене, 2 точки |
| М_30 | Прихожая (8), стена Г | по основанию — см. таблицу крепежа | окраска | 5 | анкер 5 шт., шаг 475 | уголки 2 шт. |

## Крепёж по основанию стены

| Основание стены | Крепёж |
|---|---|
| бетон, ж/б | анкер-шуруп 7,5×72 или дюбель 8×60 с шурупом 5×70 |
| кирпич полнотелый | дюбель 8×80 с шурупом 5×90 |
| газобетон, пазогребень | дюбель для газобетона 10×100 или химический анкер |
| гипсокартон | закладная до обшивки (брус 40×80 или фанера 18 мм), саморез в закладную |


## Условные обозначения

- × — анкер / уголок крепления к стене
- прямоугольник — корпус и полки ЛДСП (вид на стену)
- штриховка — компенсатор — короб до потолка

## Примечания

1. Установочные размеры — от чистого пола и чистых стен; перед установкой контрольный замер после отделки.
2. Порядок: корпус выставить по уровню опорами цоколя → закрепить к стене по задней планке → навесить двери и фасады, отрегулировать зазоры → подогнать и закрепить компенсатор.
3. Анкеры — с шагом не более 500 мм, не ближе 50 мм от края планки; на ГКЛ только в закладную, установленную до обшивки.
4. Скрытые коммуникации под анкеры проверить детектором; трассы электрики по плану розеток.
5. Монтажная схема на 2 листах, лист 2 из 2. Условные обозначения, таблица крепежа по основанию и примечания повторены на каждом листе.

| | | | | | | |
|---|---|---|---|---|---|---|
| | | | | | Проект: Квартира с кабинетом | М 1:40 |
| | Лист | № док. | Подпись | Дата | | |
| Дизайнер | Кырлан А.С. | | | 04.11.26 | Шкафы. Монтажная схема. Лист 2 из 2 | Стадия: П; Лист: 34; Листов: 127 |

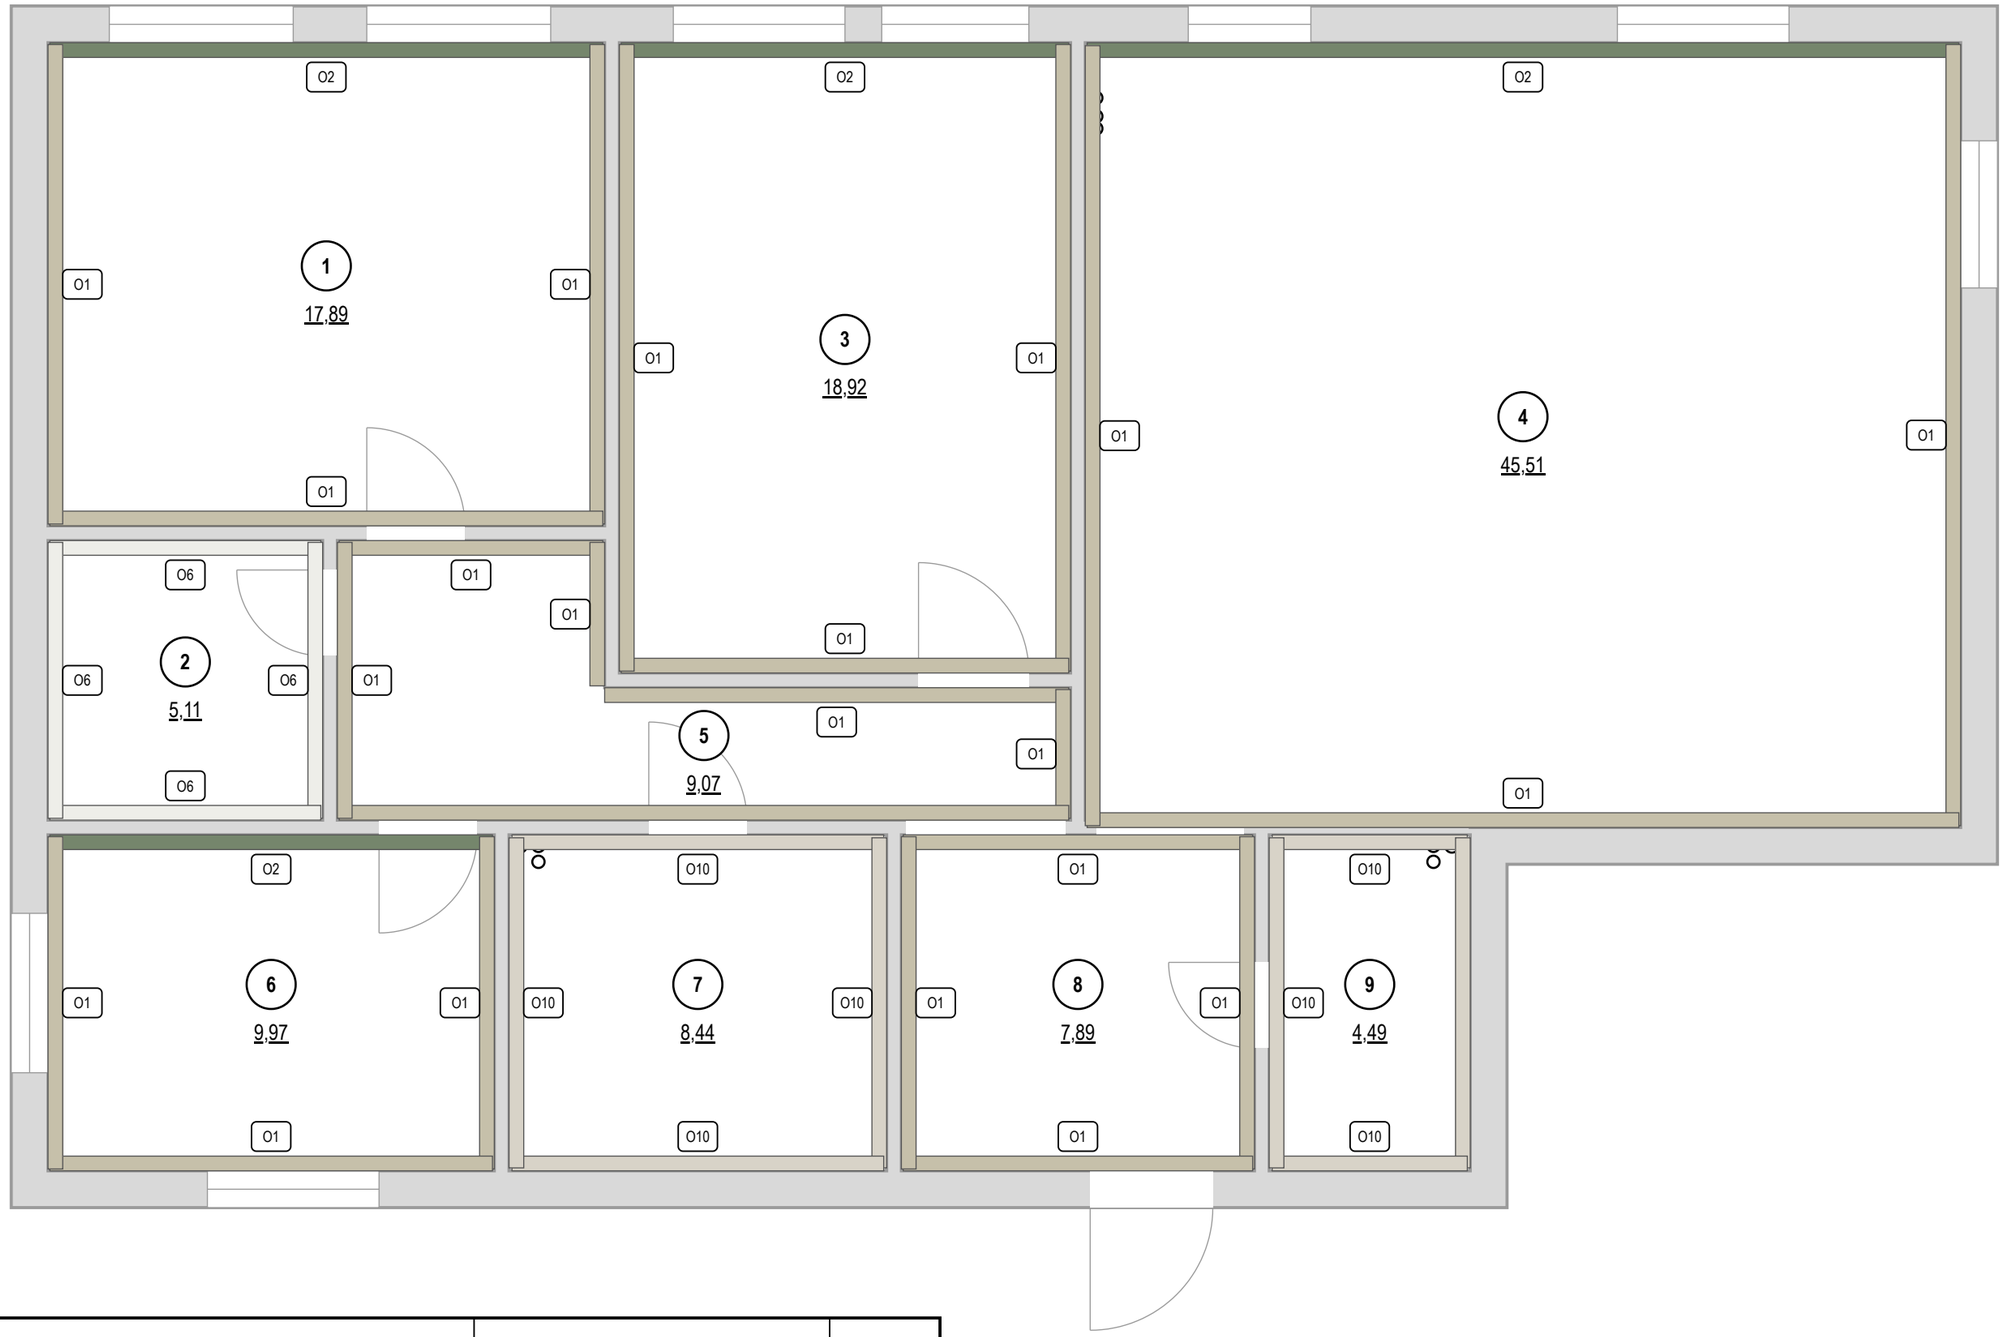


## Покрытия стен

| Марка | Покрытие | Помещение: S, м² | Итого, м² |
|---|---|---|---|
| O1 | окраска Farrow & Ball · No. 15 «Bone — мягкий каменно-серый с зеленцой» | 1: 29,1; 3: 32,8; 4: 47,8; 5: 31,4; 6: 18,9; 8: 20,1 | 180,1 |
| O2 | окраска Farrow & Ball · No. 34 «Calke Green — традиционный шалфей» | 1: 6,9; 3: 5,3; 4: 14,4; 6: 7,3 | 34,0 |
| O6 | окраска Tikkurila · V503 «Winter» | 2: 22,6 | 22,6 |
| O10 | облицовка плиткой Atlas Concorde · A8UZ «Marvel Travertine» 600×1200 мм | 7: 28,3; 9: 20,9 | 49,2 |

Площади — нетто, по развёрткам (за вычетом проёмов и фартука); высоты помещений — от чистого пола.

| | | | | | |
|---|---|---|---|---|---|
| | | | | | Проект: Квартира с кабинетом — **М 1:50** |
| | Лист | № док. | Подпись | Дата | Карта покрытий стен — Стадия: П; Лист: 35; Листов: 127 |
| Дизайнер | Кырлан А.С. | | | 04.11.26 | |

## Колерная карта по помещениям

| Помещение | Поверхность | Образец | Поз. | Система и код цвета | Производитель, линейка / материал, артикул | Блеск | Класс истирания | LRV | Площадь |
|---|---|---|---|---|---|---|---|---|---|
| **1. Спальня** 17,89 м² | стены | | **K1** | Farrow & Ball No. 15 | Farrow & Ball · Modern Emulsion | матовая | 1 | 53 | 29,4 м² |
| | акцент А | | **K2** | Farrow & Ball No. 34 | Farrow & Ball · Modern Emulsion | матовая | 1 | 22 | 6,5 м² |
| | потолок | | **K3** | Tikkurila V503 | Tikkurila · Anti-Reflex 2 | глубокомат. | 2 | 86 | 17,9 м² |
| | пол | | **KM1** | по образцу | Coswick · Вековые традиции · арт. 1167-4250 | | | | 17,9 м² |
| | плинтус | | **K4** | Farrow & Ball No. 15 | МДФ · в цвет Farrow & Ball | | | 53 | 16,2 м |
| **2. Гардеробная-постирочная** 5,11 м² | стены | | **K5** | Tikkurila V503 | Tikkurila · Harmony | матовая | 1 | 86 | 22,9 м² |
| | потолок | | **K3** | Tikkurila V503 | Tikkurila · Anti-Reflex 2 | глубокомат. | 2 | 86 | 5,1 м² |
| | пол | | **KM1** | по образцу | Coswick · Вековые традиции · арт. 1167-4250 | | | | 5,1 м² |
| | плинтус | | **K6** | Tikkurila V503 | МДФ · в цвет Tikkurila | | | 86 | 8,3 м |
| **3. Кабинет** 18,92 м² | стены | | **K1** | Farrow & Ball No. 15 | Farrow & Ball · Modern Emulsion | матовая | 1 | 53 | 33,0 м² |
| | акцент А | | **K2** | Farrow & Ball No. 34 | Farrow & Ball · Modern Emulsion | матовая | 1 | 22 | 5,0 м² |
| | потолок | | **K3** | Tikkurila V503 | Tikkurila · Anti-Reflex 2 | глубокомат. | 2 | 86 | 18,9 м² |
| | пол | | **KM1** | по образцу | Coswick · Вековые традиции · арт. 1167-4250 | | | | 18,9 м² |
| | плинтус | | **K4** | Farrow & Ball No. 15 | МДФ · в цвет Farrow & Ball | | | 53 | 16,7 м |
| **4. Кухня-гостиная** 45,51 м² | стены | | **K1** | Farrow & Ball No. 15 | Farrow & Ball · Modern Emulsion | матовая | 1 | 53 | 46,7 м² |
| | акцент А | | **K2** | Farrow & Ball No. 34 | Farrow & Ball · Modern Emulsion | матовая | 1 | 22 | 14,9 м² |
| | потолок | | **K3** | Tikkurila V503 | Tikkurila · Anti-Reflex 2 | глубокомат. | 2 | 86 | 45,5 м² |
| | пол | | **KM1** | по образцу | Coswick · Вековые традиции · арт. 1167-4250 | | | | 45,5 м² |
| | плинтус | | **K4** | Farrow & Ball No. 15 | МДФ · в цвет Farrow & Ball | | | 53 | 25,9 м |
| | фартук | | **KM2** | по образцу | керамогранит · аналог по хар. | | | | 0,7 м² |
| **5. Коридор** 9,07 м² | стены | | **K1** | Farrow & Ball No. 15 | Farrow & Ball · Modern Emulsion | матовая | 1 | 53 | 31,8 м² |
| | потолок | | **K3** | Tikkurila V503 | Tikkurila · Anti-Reflex 2 | глубокомат. | 2 | 86 | 9,1 м² |
| | пол | | **KM1** | по образцу | Coswick · Вековые традиции · арт. 1167-4250 | | | | 9,1 м² |
| | плинтус | | **K4** | Farrow & Ball No. 15 | МДФ · в цвет Farrow & Ball | | | 53 | 11,2 м |
| **6. Детская** 9,97 м² | стены | | **K1** | Farrow & Ball No. 15 | Farrow & Ball · Modern Emulsion | матовая | 1 | 53 | 18,5 м² |
| | акцент А | | **K2** | Farrow & Ball No. 34 | Farrow & Ball · Modern Emulsion | матовая | 1 | 22 | 7,4 м² |
| | потолок | | **K3** | Tikkurila V503 | Tikkurila · Anti-Reflex 2 | глубокомат. | 2 | 86 | 10,0 м² |
| | пол | | **KM1** | по образцу | Coswick · Вековые традиции · арт. 1167-4250 | | | | 10,0 м² |
| | плинтус | | **K7** | Farrow & Ball No. 15 | Orac Decor · Contour (Luxxus) | | | 53 | 12,0 м |
| **7. Ванная** 8,44 м² | стены | | **KM3** | Marvel Travertine | Atlas Concorde · арт. A8UZ | | | | 28,8 м² |
| | потолок | | **K8** | Tikkurila V503 | Tikkurila · Luja 7 | матовая | 1 | 86 | 8,4 м² |
| | пол | | **KM4** | по образцу | керамогранит · аналог по хар. | | | | 8,4 м² |
| **8. Прихожая** 7,89 м² | стены | | **K1** | Farrow & Ball No. 15 | Farrow & Ball · Modern Emulsion | матовая | 1 | 53 | 20,4 м² |
| | потолок | | **K3** | Tikkurila V503 | Tikkurila · Anti-Reflex 2 | глубокомат. | 2 | 86 | 7,9 м² |
| | пол | | **KM5** | Marvel Travertine | Atlas Concorde · арт. A8UZ | | | | 7,9 м² |
| | плинтус | | **K4** | Farrow & Ball No. 15 | МДФ · в цвет Farrow & Ball | | | 53 | 7,0 м |
| **9. Санузел гостевой** 4,49 м² | стены | | **KM3** | Marvel Travertine | Atlas Concorde · арт. A8UZ | | | | 21,4 м² |
| | потолок | | **K8** | Tikkurila V503 | Tikkurila · Luja 7 | матовая | 1 | 86 | 4,5 м² |
| | пол | | **KM4** | по образцу | керамогранит · аналог по хар. | | | | 4,5 м² |

## Примечания

1. Цвет на листе и на экране — ориентир. До покраски — выкрас на объекте: не меньше А3 (или лист ГКЛ), на грунте под эту краску, не на белой шпаклёвке, в 2 слоя; на обороте — код, бренд, веер, дата. Смотреть днём и вечером, рядом с образцами пола и плитки; к основному цвету стен — ещё 2 соседних оттенка. Красить только в цвет утверждённого выкраса.
2. Краску заказывать по коду из графы «Система и код цвета» у бренда этого кода, не «аналогом» другого; весь объём одного кода — одной партией, колеруемую краску — за один проход машины.
3. Площади — те же, что в ведомости отделки (лист С1); сколько краски заказать — в спецификации отделочных материалов (лист С3).

## Схема палитры проекта

Стиль: Модерн (ар-нуво) 60% + Современный (контемпорари) 40% · схема: аналоговая

| основной | основной | второстепенный | второстепенный | акцентный | акцентный | акцентный |
|---|---|---|---|---|---|---|
| **Farrow & Ball No. 15** | **Tikkurila V503** | **Farrow & Ball No. 34** | **Farrow & Ball No. 286** | **NCS S 5030-B10G** | **Farrow & Ball No. 66** | **NCS S 8010-Y30R** |
| Bone — мягкий каменно-серый с зеленцой<br>LRV 53<br>стены 1,3,4,5,6,8; плинтус 1,3,4,5,6,8 | Winter<br>LRV 86<br>потолок 1,2,3,4,5,6,7,8,9; стены 2; плинтус 2; текстиль/декор 1,3,4,6 | Calke Green — традиционный шалфей<br>LRV 22<br>акцент 1,3,4,6; текстиль/декор 1,3,4,6 | Peignoir — серо-розовый<br>LRV 57<br>текстиль/декор 3,6 | Павлиний сине-зелёный<br>LRV 12<br>текстиль/декор 3,6 | India Yellow — глубокая горчица<br>LRV 36<br>текстиль/декор 3,4,6 | Тёмно-коричневый<br>LRV 3<br>в отделке не применён |

План 60/30/10




Окраска, факт — по площади стен, акцентов, потолков




окрашено всего 364 м²; второстепенный тон несут мебель и текстиль

**Текстиль и декор в цветах вне палитры проекта**

- NCS S 2010-Y30R Тёплый льняной беж — пом. 1 (T1, T27, T4), 3 (T7), 4 (T13, T17), 6 (T20)
- NCS S 5020-G50Y Оливковый — пом. 1 (T3)

## Условные обозначения

- **K1** Farrow & Ball No. 15 · Bone — мягкий каменно-серый с зеленцой · Modern Emulsion · матовая · кл. 1
- **K2** Farrow & Ball No. 34 · Calke Green — традиционный шалфей · Modern Emulsion · матовая · кл. 1
- **K3** Tikkurila V503 · Winter · Anti-Reflex 2 · глубокомат. · кл. 2
- **K4** Farrow & Ball No. 15 · Bone — мягкий каменно-серый с зеленцой · МДФ
- **K5** Tikkurila V503 · Winter · Harmony · матовая · кл. 1
- **K6** Tikkurila V503 · Winter · МДФ
- **K7** Farrow & Ball No. 15 · Bone — мягкий каменно-серый с зеленцой · Contour (Luxxus)
- **K8** Tikkurila V503 · Winter · Luja 7 · матовая · кл. 1
- дерево (доска, паркет, ламинат) — рисунок досок
- керамогранит, плитка, камень — сетка швов по формату
- **KM1** инженерная доска · 1167-4250
- **KM2** аналог: керамогранит под травертин, матовый, 1200×600×9 мм
- **KM3** плитка · A8UZ
- **KM4** аналог: керамогранит ректифицированный под травертин, матовый, 600×600×9 мм
- **KM5** керамогранит · A8UZ

К — краска, КМ — отделочный материал (тон КМ — по описанию, эталон — образец материала); кл. — класс истирания (1 — самый стойкий к мытью); LRV — светлота цвета: 0 — чёрный, 100 — белый


## Перечень выкрасов на согласование

| № | Код | Бренд / веер | Пом. / стена | Подложка | Формат | Статус |
|---|---|---|---|---|---|---|
| 1 | No. 15 | Farrow & Ball | 1, 3, 4, 5, 6, 8 | ГКЛ с грунтом; МДФ под эмаль | 600×1000; 300×600 | к выполнению |
| 2 | No. 34 | Farrow & Ball | 1 A, 3 A, 4 A, 6 A | ГКЛ с грунтом | 600×1000 | к выполнению |
| 3 | V503 | Tikkurila | 1, 2, 3, 4, 5, 6, 7, 8, 9 | ГКЛ с грунтом; МДФ под эмаль | 600×1000; 300×600 | к выполнению |

| | | | | | |
|---|---|---|---|---|---|
| | Лист | № док. | Подпись | Дата | Проект: Квартира с кабинетом |
| Дизайнер | Кырлан А.С. | | | 04.11.26 | Колерная карта |

| Стадия | Лист | Листов |
|---|---|---|
| П | 36 | 127 |

выпуск 04.11.2026 № 627e1ac6ce · стр. 36 из 127

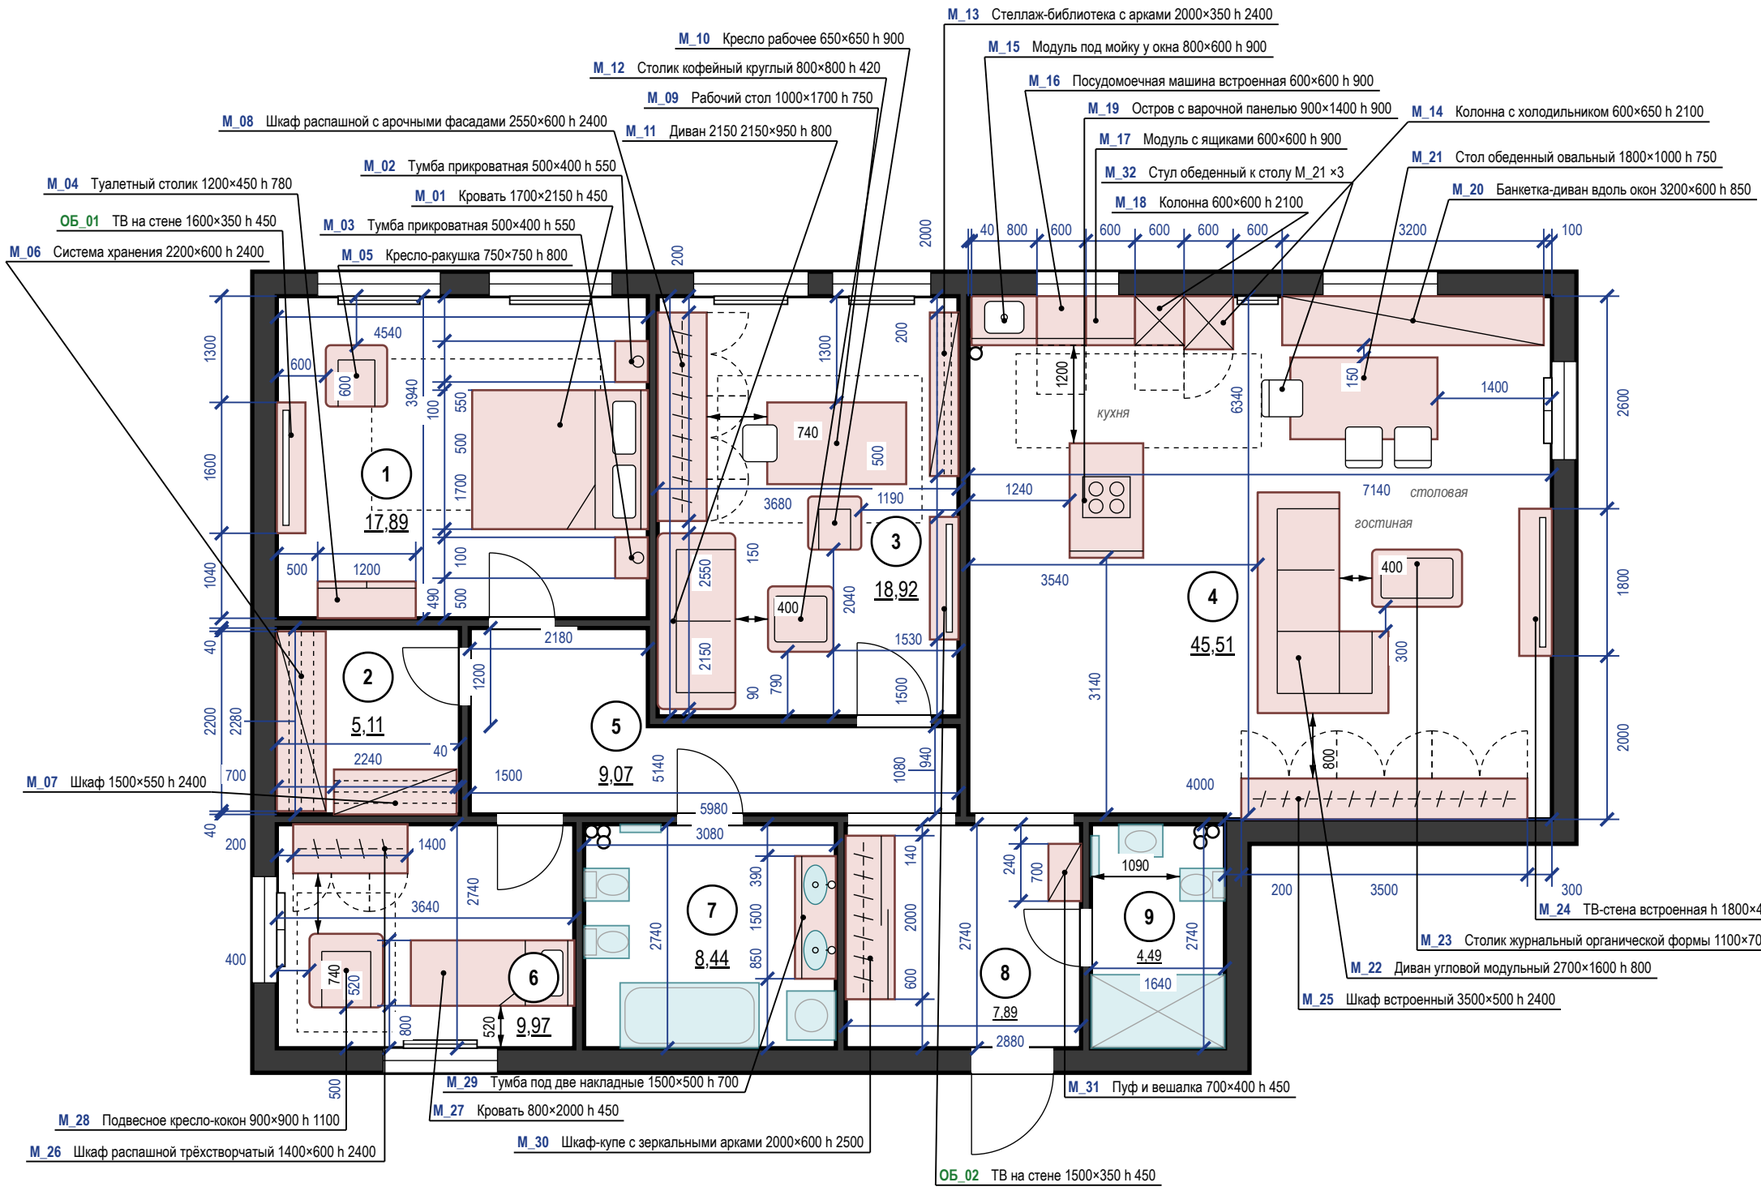


**Экспликация помещений**

лист 30 · на плане — номера в марках

## Ведомость мебели и оборудования

| Марка | Наименование | Ш×Г×В, мм | Пом. | Кол. |
|---|---|---|---|---|
| M_01 | Кровать 1700×2150 | 1700×2150×450 | 1 | 1 |
| M_02 | Тумба прикроватная | 500×400×550 | 1 | 1 |
| M_03 | Тумба прикроватная | 500×400×550 | 1 | 1 |
| ОБ_01 | ТВ на стене | 1600×350×450 | 1 | 1 |
| M_04 | Туалетный столик | 1200×450×780 | 1 | 1 |
| M_05 | Кресло-ракушка | 750×750×800 | 1 | 1 |
| M_06 | Система хранения | 2200×600×2400 | 2 | 1 |
| M_07 | Шкаф | 1500×550×2400 | 2 | 1 |
| M_08 | Шкаф распашной с арочными фасадами | 2550×600×2400 | 3 | 1 |
| M_09 | Рабочий стол 1700×1000 | 1000×1700×750 | 3 | 1 |
| M_10 | Кресло рабочее | 650×650×900 | 3 | 1 |
| M_11 | Диван 2150 | 2150×950×800 | 3 | 1 |
| M_12 | Столик кофейный круглый | 800×800×420 | 3 | 1 |
| M_13 | Стеллаж-библиотека с арками | 2000×350×2400 | 3 | 1 |
| ОБ_02 | ТВ на стене | 1500×350×450 | 3 | 1 |
| M_14 | Колонна с холодильником | 600×650×2100 | 4 | 1 |
| M_15 | Модуль под мойку у окна | 800×600×900 | 4 | 1 |
| M_16 | Посудомоечная машина встроенная | 600×600×900 | 4 | 1 |
| M_17 | Модуль с ящиками | 600×600×900 | 4 | 1 |
| M_18 | Колонна | 600×600×2100 | 4 | 1 |
| M_19 | Остров 900×1400 с варочной панелью | 900×1400×900 | 4 | 1 |
| M_20 | Банкетка-диван вдоль окон | 3200×600×850 | 4 | 1 |
| M_21 | Стол обеденный овальный 1800×1000 | 1800×1000×750 | 4 | 1 |
| M_22 | Диван угловой модульный | 2700×1600×800 | 4 | 1 |
| M_23 | Столик журнальный органической формы | 1100×700×380 | 4 | 1 |
| M_24 | ТВ-стена встроенная h 1800×400 h | 1800×400×2500 | 4 | 1 |
| M_25 | Шкаф встроенный | 3500×500×2400 | 4 | 1 |
| M_26 | Шкаф распашной трёхстворчатый | 1400×600×2400 | 6 | 1 |
| M_27 | Кровать 800×2000 | 800×2000×450 | 6 | 1 |
| M_28 | Подвесное кресло-кокон | 900×900×1100 | 6 | 1 |
| M_29 | Тумба под две накладные | 1500×500×700 | 7 | 1 |
| M_30 | Шкаф-купе с зеркальными арками | 2000×600×2500 | 8 | 1 |
| M_31 | Пуф и вешалка | 700×400×450 | 8 | 1 |
| M_32 | Стул обеденный к столу M_21 | 450×500×820 | 4 | 3 |

Ш — вдоль стены (изголовья), Г — от стены (длина кровати)

Материалы, модели, допуск замены — лист 38

### Примечания

1. Размеры — в мм от чистовых поверхностей стен; размеры мебели уточнить после отделочных работ; общие указания — лист 27.
2. Стулья обеденной группы (M_32 — 3 шт.) показаны в рабочем положении, задвинутыми под столешницу на 150 мм.

| | | | | | | |
|---|---|---|---|---|---|---|
| | | | | | Проект: Квартира с кабинетом | M 1:75 |
| | Лист | № док. | Подпись | Дата | | |
| Дизайнер | Кырлан А.С. | | | 04.11.26 | План размещения мебели и оборудования | Стадия: П; Лист: 37; Листов: 127 |

| Поз. | Наименование и техническая характеристика | Тип, марка, обозначение документа, опросного листа | Код продукции | Поставщик | Ед. измерения | Кол. | Масса 1 ед., кг | Примечание |
|---|---|---|---|---|---|---|---|---|
| | **Мебель встроенная и корпусная (изготовление по чертежам мебельщика)** | | | | | | | |
| M_06 | Система хранения: штанги, полки, ящики; каркас и полки — ЛДСП 16 мм, декор «дуб натуральный»; без фасадов; Ш×Г×В 2200×600×2400 мм | | | изготовление на заказ | шт. | 1 | | пом. 2; крепление к стене |
| M_07 | Шкаф с выдвижной гладильной доской и полками; каркас и полки — ЛДСП 16 мм, декор «дуб натуральный»; без фасадов; Ш×Г×В 1500×550×2400 мм | | | изготовление на заказ | шт. | 1 | | пом. 2; крепление к стене |
| M_08 | Шкаф распашной с арочными фасадами; корпус ЛДСП 16 мм; фасады — МДФ 18 мм, эмаль матовая; арочная фрезеровка филёнки (полукруглый верх, поле 100 мм); Ш×Г×В 2550×600×2400 мм | | | изготовление на заказ | шт. | 1 | | пом. 3 |
| M_14 | Колонна с холодильником; корпус ЛДСП 16 мм; фасады — МДФ 18 мм, эмаль матовая; цвет фасадов — в цвет стен (Farrow & Ball No. 15); Ш×Г×В 600×650×2100 мм | | | изготовление на заказ | шт. | 1 | | пом. 4 |
| M_15 | Модуль под мойку у окна; корпус ЛДСП 16 мм; фасады — МДФ 18 мм, эмаль матовая; цвет фасадов — в цвет стен (Farrow & Ball No. 15); Ш×Г×В 800×600×900 мм | | | изготовление на заказ | шт. | 1 | | пом. 4 |
| M_16 | Модуль под встраиваемую ПММ 60; без корпуса (ниша между соседними модулями); фасад на дверь машины — МДФ 18 мм, эмаль матовая; цоколь; цвет фасадов — в цвет стен (Farrow & Ball No. 15); Ш×Г×В 600×600×900 мм | | | изготовление на заказ | шт. | 1 | | пом. 4 |
| M_17 | Модуль с ящиками; корпус ЛДСП 16 мм; фасады — МДФ 18 мм, эмаль матовая; цвет фасадов — в цвет стен (Farrow & Ball No. 15); Ш×Г×В 600×600×900 мм | | | изготовление на заказ | шт. | 1 | | пом. 4 |
| M_18 | Колонна: духовой шкаф и СВЧ; корпус ЛДСП 16 мм; фасады — МДФ 18 мм, эмаль матовая; цвет фасадов — в цвет стен (Farrow & Ball No. 15); Ш×Г×В 600×600×2100 мм | | | изготовление на заказ | шт. | 1 | | пом. 4 |
| M_19 | Остров 900×1400 с варочной панелью, столешница — травертин; корпус ЛДСП 16 мм; фасады — МДФ 18 мм, эмаль матовая; цвет фасадов — в цвет стен (Farrow & Ball No. 15); Ш×Г×В 900×1400×900 мм | | | изготовление на заказ | шт. | 1 | | пом. 4 |
| M_20 | Банкетка-диван вдоль окон, бархат — экран радиатора, изготовление на заказ; Ш×Г×В 3200×600×850 мм | | | изготовление на заказ | шт. | 1 | | пом. 4 |
| M_24 | ТВ-стена встроенная 1800×400 h 2500: каркас на стене Б, панели МДФ с волнистым рельефом (эмаль), ниша ТВ 1500×900 на отметке +900 (низ), ниша биокамина 900×400 на отметке +350 (низ), облицовка ниши камина — негорючая (сталь / камень), вентиляционные зазоры 50 мм над топкой; корпус оцинкованный профиль ПП 60×27 / ПН 28×27 (НГ), на стене Б 27 мм; фасады — панели МДФ 19 мм с волнистым рельефом, эмаль матовая; Ш×Г×В 1800×400×2500 мм | | | изготовление на заказ | шт. | 1 | | пом. 4 |
| M_25 | Шкаф встроенный, фасады с округлыми торцами; корпус ЛДСП 16 мм; фасады — МДФ 18 мм, эмаль матовая; цвет фасадов — в цвет стен (Farrow & Ball No. 15); Ш×Г×В 3500×500×2400 мм | | | изготовление на заказ | шт. | 1 | | пом. 4 |
| M_26 | Шкаф распашной трёхстворчатый с антресолью; корпус ЛДСП 16 мм; фасады — МДФ 18 мм, эмаль матовая; цвет фасадов в цвет стен (Farrow & Ball No. 15); Ш×Г×В 1400×600×2400 мм | | | изготовление на заказ | шт. | 1 | | пом. 6; крепление к стене |
| M_29 | Тумба под две накладные раковины C_02, C_03, 1500 мм, напольная; корпус ЛДСП 16 мм; фасады — МДФ 18 мм, эмаль матовая; цвет фасадов — в цвет стен (Atlas Concorde A8UZ); Ш×Г×В 1500×500×700 мм | | | изготовление на заказ | шт. | 1 | | пом. 7; крепление к стене |
| M_30 | Шкаф-купе с зеркальными арками; корпус ЛДСП 16 мм; фасады — МДФ 10 мм, эмаль матовая в профиле: алюминий, латунь матовая; вставка — зеркало серебро 4 мм, плёнка безопасности, арочная (полукруглый верх, поле 100 мм); Ш×Г×В 2000×600×2500 мм | | | изготовление на заказ | шт. | 1 | | пом. 8 |
| | **Мебель покупная** | | | | | | | |
| M_01 | Кровать 1700×2150 с высоким округлым изголовьем, бархат; мягкое изголовье, обивка — ткань, цвет Farrow & Ball No. 34; Ш×Г×В 1700×2150×450 мм | | | аналог по характеристикам | шт. | 1 | | пом. 1; замена ≤ габарита |
| M_02, M_03 | Тумба прикроватная, морёный дуб, латунные ручки; шпон, дуб натуральный, матовое масло; Ш×Г×В 500×400×550 мм | | | аналог по характеристикам | шт. | 2 | | пом. 1; замена ≤ габарита |
| M_04 | Туалетный столик с овальным зеркалом в латунной раме; шпон, дуб натуральный, матовое масло; Ш×Г×В 1200×450×780 мм | | | аналог по характеристикам | шт. | 1 | | пом. 1; замена ≤ габарита |
| M_05 | Кресло-ракушка, бархат павлиньего цвета; обивка — ткань, цвет Farrow & Ball No. 34; Ш×Г×В 750×750×800 мм | | | аналог по характеристикам | шт. | 1 | | пом. 1; замена ≤ габарита |
| ОБ_01 | ТВ на стене, тумба подвесная с волнистым фасадом; шпон, дуб натуральный, матовое масло; Ш×Г×В 1600×350×450 мм | | | аналог по характеристикам | шт. | 1 | | пом. 1; замена ≤ габарита |
| M_09 | Рабочий стол 1700×1000, морёный дуб, округлые углы; шпон, дуб натуральный, матовое масло; Ш×Г×В 1000×1700×750 мм | | | аналог по характеристикам | шт. | 1 | | пом. 3; замена ≤ габарита |

## Примечания

1. Позиции мебели совпадают с марками на плане расстановки; размеры Ш×Г×В — Ш вдоль стены, Г от стены.
2. Размеры и привязки плана расстановки — в мм от чистовых поверхностей стен: слой штукатурки 20 мм по блоку и 5 мм шпаклёвки по ГКЛ учтён; привязки — от стен и углов помещения, а не от другой мебели.
3. План расстановки не является документацией для изготовления мебели. Встроенная и корпусная мебель изготавливается по чертежам мебельщика после контрольного обмера (после штукатурки); «стена в стену» — с зазором 10 мм с каждой стороны или с компенсаторами; графы «Тип, марка» и «Код продукции» для неё не заполняются (ГОСТ 21.110-2013).
4. Покупные изделия — аналог по характеристикам: заменять только на изделия не больше указанного габарита и того же материала и цвета.
5. Материал и цвет, не указанные в данных изделия, приняты по концепции: тон дерева — по полу, обивка — по вторичному цвету палитры; образцы согласовать до заказа.
6. Масса 1 ед. для изделий до 25 кг не указывается. Техника — по монтажным схемам изготовителя; выводы — по листам ЭОМ и ВК.

| | | | | | |
|---|---|---|---|---|---|
| | | | | | Проект: Квартира с кабинетом |
| | Лист | № док. | Подпись | Дата | Спецификация мебели и оборудования |
| Дизайнер | Кырлан А.С. | | | 04.11.26 | Стадия: П; Лист: 38; Листов: 127 |

| Поз. | Наименование и техническая характеристика | Тип, марка, обозначение документа, опросного листа | Код продукции | Поставщик | Ед. измерения | Кол. | Масса 1 ед., кг | Примечание |
|---|---|---|---|---|---|---|---|---|
| M_10 | Кресло рабочее, кожа карамельного цвета; обивка — ткань, цвет Farrow & Ball No. 34; Ш×Г×В 650×650×900 мм | | | аналог по характеристикам | шт. | 1 | | пом. 3; замена ≤ габарита |
| M_11 | Диван 2150 с мягкими округлыми подлокотниками; обивка — ткань, цвет Farrow & Ball No. 34; Ш×Г×В 2150×950×800 мм | | | аналог по характеристикам | шт. | 1 | | пом. 3; замена ≤ габарита |
| M_12 | Столик кофейный круглый, травертин; шпон, дуб натуральный, матовое масло; Ш×Г×В 800×800×420 мм | | | аналог по характеристикам | шт. | 1 | | пом. 3; замена ≤ габарита |
| M_13 | Стеллаж-библиотека с арками; шпон, дуб натуральный, матовое масло; Ш×Г×В 2000×350×2400 мм | | | аналог по характеристикам | шт. | 1 | | пом. 3; замена ≤ габарита |
| ОБ_02 | ТВ на стене, тумба подвесная; шпон, дуб натуральный, матовое масло; Ш×Г×В 1500×350×450 мм | | | аналог по характеристикам | шт. | 1 | | пом. 3; замена ≤ габарита |
| M_21 | Стол обеденный овальный 1800×1000, морёный дуб; шпон, дуб натуральный, матовое масло; Ш×Г×В 1800×1000×750 мм | | | аналог по характеристикам | шт. | 1 | | пом. 4; замена ≤ габарита |
| M_22 | Диван угловой модульный с округлыми формами, бархат павлиньего цвета; Г-образный: основная секция 2700, вторая 1000 × 1600 мм; обивка — ткань, цвет Farrow & Ball No. 34; Ш×Г×В 2700×1600×800 мм | | | аналог по характеристикам | шт. | 1 | | пом. 4; замена ≤ габарита |
| M_23 | Столик журнальный органической формы, травертин; шпон, дуб натуральный, матовое масло; Ш×Г×В 1100×700×380 мм | | | аналог по характеристикам | шт. | 1 | | пом. 4; замена ≤ габарита |
| M_32 | Стул обеденный к столу M_21; обивка — ткань, цвет Farrow & Ball No. 34; каркас — дуб натуральный; Ш×Г×В 450×500×820 мм | | | аналог по характеристикам | шт. | 3 | | пом. 4; замена ≤ габарита |
| M_27 | Кровать 800×2000 с мягким изголовьем-облаком; мягкое изголовье, обивка — ткань, цвет Farrow & Ball No. 34; Ш×Г×В 800×2000×450 мм | | | аналог по характеристикам | шт. | 1 | | пом. 6; замена ≤ габарита |
| M_28 | Подвесное кресло-кокон; обивка — ткань, цвет Farrow & Ball No. 34; Ш×Г×В 900×900×1100 мм | | | аналог по характеристикам | шт. | 1 | | пом. 6; замена ≤ габарита |
| M_31 | Пуф и вешалка; Ш×Г×В 700×400×450 мм | | | аналог по характеристикам | шт. | 1 | | пом. 8; замена ≤ габарита |
| | **Техника встраиваемая и бытовая (покупные изделия), светильники под розетки** | | | | | | | |
| | Холодильник встраиваемый, в модуле M_14 | аналог по характеристикам: полновстраиваемый под фасад, ниша 1780 × 560 × 550 мм, вентиляция решётка в цоколе, выход сверху | | по выбору заказчика до изготовления мебели | шт. | 1 | | пом. 4; по схеме изготовителя |
| | Посудомоечная машина встраиваемая, в модуле M_16; ниша 600 мм | аналог по характеристикам: полновстраиваемая 60 см под фасад, ниша 600 × 862 мм, навеска фасада в комплекте | | по выбору заказчика до изготовления мебели | шт. | 1 | | пом. 4; по схеме изготовителя |
| | Духовой шкаф встраиваемый, в модуле M_18 | аналог по характеристикам: 60 см, лицевая панель 595 мм, ниша 568 × 600, глубина ≥ 550 мм, вентиляция за прибором | | по выбору заказчика до изготовления мебели | шт. | 1 | | пом. 4; по схеме изготовителя |
| | СВЧ-печь встраиваемая, в модуле M_18 | аналог по характеристикам: встраиваемая 38 см, лицевая панель 388 мм, ниша 568 × 380, глубина ≥ 550 мм | | по выбору заказчика до изготовления мебели | шт. | 1 | | пом. 4; по схеме изготовителя |
| | Вытяжка, над островом M_19, потолочная, 900 мм, рециркуляция (угольный фильтр), низ +1,550 | аналог по характеристикам: производительность — по расчёту ОВ, шум ≤ 55 дБ(А) | | по выбору заказчика до изготовления мебели | шт. | 1 | | пом. 4; по схеме изготовителя |
| | Варочная панель встраиваемая, индукционная, в модуле M_19 | аналог по характеристикам: индукционная 60 см, вырез 560 × 490 мм по шаблону модели | | по выбору заказчика до изготовления мебели | шт. | 1 | | пом. 4; по схеме изготовителя |
| | Стиральная машина, место по листу ВК (ОБ_03); Ш×Г 600×600 мм | аналог по характеристикам: тип загрузки — по листу ВК, в плане 600 × 600 мм (ширина × глубина), по листу ВК | | по выбору заказчика до изготовления мебели | шт. | 1 | | пом. 7; по схеме изготовителя |
| | Торшер, у поз. ОБ_01; абажур — ткань или опаловое стекло; лампа 2700 K | | | аналог по характеристикам | шт. | 1 | | пом. 1; розетка P5 (ЭОМ) |
| | **Текстиль** | | | | | | | |
| T1 | Портьеры-волна; лён 100 %; цвет NCS S 2010-Y30R; карниз 2300 мм, высота 2590 мм, сборка 2 | | | аналог по характеристикам | шт. | 2 | | пом. 1 |
| T2 | Тюль; полиэстер 100 %; цвет Tikkurila V503; карниз 2300 мм, высота 2590 мм, сборка 2,5 | | | аналог по характеристикам | шт. | 1 | | пом. 1 |
| T27 | Портьеры-волна; лён 100 %; цвет NCS S 2010-Y30R; карниз 2300 мм, высота 2590 мм, сборка 2 | | | аналог по характеристикам | шт. | 2 | | пом. 1 |
| T28 | Тюль; полиэстер 100 %; цвет Tikkurila V503; карниз 2300 мм, высота 2590 мм, сборка 2,5 | | | аналог по характеристикам | шт. | 1 | | пом. 1 |
| T3 | Ковёр под кроватью; шерсть 80 %, хлопок 20 %; цвет NCS S 5020-G50Y; 2800×1850 мм | | | аналог по характеристикам | шт. | 1 | | пом. 1; с подложкой |
| T4 | Подушки декоративные на кровать; лён 100 %; цвет NCS S 2010-Y30R | | | аналог по характеристикам | шт. | 3 | | пом. 1 |
| T5 | Подушки на кровать, акцент; хлопковый бархат 100 %; цвет Farrow & Ball No. 34 | | | аналог по характеристикам | шт. | 2 | | пом. 1 |
| T6 | Плед на кровать; шерсть мериноса 100 %; цвет Farrow & Ball No. 34 | | | аналог по характеристикам | шт. | 1 | | пом. 1 |



| | | | | | |
|---|---|---|---|---|---|
| | | | | | Проект: Квартира с кабинетом |
| | Лист | № док. | Подпись | Дата | |
| Дизайнер | Кырлан А.С. | | | 04.11.26 | Спецификация мебели и оборудования (продолжение) |

| Стадия | Лист | Листов |
|---|---|---|
| П | 39 | 127 |

| Поз. | Наименование и техническая характеристика | Тип, марка, обозначение документа, опросного листа | Код продукции | Поставщик | Ед. измерения | Кол. | Масса 1 ед., кг | Примечание |
|---|---|---|---|---|---|---|---|---|
| Т7 | Портьеры-волна; лён 100 %; цвет NCS S 2010-Y30R; карниз 1820 мм, высота 2590 мм, сборка 2 | | | аналог по характеристикам | шт. | 2 | | пом. 3 |
| Т8 | Тюль; полиэстер 100 %; цвет Tikkurila V503; карниз 1820 мм, высота 2590 мм, сборка 2,5 | | | аналог по характеристикам | шт. | 1 | | пом. 3 |
| Т9 | Ковёр под кроватью; шерсть 100 %; цвет Farrow & Ball No. 66; 2500×1800 мм | | | аналог по характеристикам | шт. | 1 | | пом. 3; с подложкой |
| Т10 | Подушки декоративные на кровать; букле (шерсть 60 %, полиэстер 40 %); цвет Farrow & Ball No. 286 | | | аналог по характеристикам | шт. | 3 | | пом. 3 |
| Т11 | Подушки на кровать, акцент; хлопковый бархат 100 %; цвет NCS S 5030-B10G | | | аналог по характеристикам | шт. | 2 | | пом. 3 |
| Т12 | Плед на кровать; шерсть мериноса 100 %; цвет Farrow & Ball No. 34 | | | аналог по характеристикам | шт. | 1 | | пом. 3 |
| Т13 | Портьеры-волна (гостиная); лён 70 %, вискоза 30 %; цвет NCS S 2010-Y30R; карниз 1650 мм, высота 2690 мм, сборка 2 | | | аналог по характеристикам | шт. | 2 | | пом. 4 |
| Т14 | Тюль (гостиная); полиэстер 100 %; цвет Tikkurila V503; карниз 1650 мм, высота 2690 мм, сборка 2,5 | | | аналог по характеристикам | шт. | 1 | | пом. 4 |
| Т15 | Римская штора (кухня); лён 100 %; цвет Farrow & Ball No. 66; карниз 1400 мм, высота 1700 мм | | | аналог по характеристикам | шт. | 1 | | пом. 4 |
| Т26 | Римская штора (кухня, окно над рабочей зоной); лён 100 %; цвет Farrow & Ball No. 66; карниз 1000 мм, высота 1700 мм | | | аналог по характеристикам | шт. | 1 | | пом. 4 |
| Т16 | Ковёр в зоне отдыха; шерсть 100 %; цвет Farrow & Ball No. 66; 3000×1150 мм | | | аналог по характеристикам | шт. | 1 | | пом. 4; с подложкой |
| Т17 | Подушки на диван; букле (шерсть 60 %, полиэстер 40 %); цвет NCS S 2010-Y30R | | | аналог по характеристикам | шт. | 3 | | пом. 4 |
| Т18 | Подушки на диван, акцент; хлопковый бархат 100 %; цвет Farrow & Ball No. 34 | | | аналог по характеристикам | шт. | 2 | | пом. 4 |
| Т19 | Плед на диван; альпака 50 %, шерсть 50 %; цвет Farrow & Ball No. 66 | | | аналог по характеристикам | шт. | 1 | | пом. 4 |
| Т20 | Портьеры-волна; лён 100 %; цвет NCS S 2010-Y30R; карниз 1820 мм, высота 2590 мм, сборка 2 | | | аналог по характеристикам | шт. | 2 | | пом. 6 |
| Т21 | Тюль; полиэстер 100 %; цвет Tikkurila V503; карниз 1820 мм, высота 2590 мм, сборка 2,5 | | | аналог по характеристикам | шт. | 1 | | пом. 6 |
| Т22 | Ковёр у кресла-кокона (зона чтения); шерсть 100 %; цвет Farrow & Ball No. 66; 1200×1700 мм | | | аналог по характеристикам | шт. | 1 | | пом. 6; с подложкой |
| Т23 | Подушки декоративные на кровать; букле (шерсть 60 %, полиэстер 40 %); цвет Farrow & Ball No. 286 | | | аналог по характеристикам | шт. | 3 | | пом. 6 |
| Т24 | Подушки на кровать, акцент; хлопковый бархат 100 %; цвет NCS S 5030-B10G | | | аналог по характеристикам | шт. | 2 | | пом. 6 |
| Т25 | Плед на кровать; шерсть мериноса 100 %; цвет Farrow & Ball No. 34 | | | аналог по характеристикам | шт. | 1 | | пом. 6 |
| | **Декор** | | | | | | | |
| ДК1 | Картина над кроватью: абстракция, холст, тонкая рама из дуба; 1200×700 мм; низ на 1300 мм от пола | | | аналог по характеристикам | шт. | 1 | 4 | пом. 1; крепление к стене |
| ДК3 | Картина над диваном: графика в паспарту, рама — дуб; 1400×700 мм; низ на 1000 мм от пола | | | аналог по характеристикам | шт. | 1 | 4 | пом. 3; крепление к стене |
| ДК4 | Зеркало в рост в тонкой чёрной раме; рама — чёрный матовый; 600×1600 мм; низ на 300 мм от пола | | | аналог по характеристикам | шт. | 1 | 12 | пом. 3; крепление: анкер для пустотелых оснований, 4 шт. |
| ДК6 | Картина: крупная абстракция в тёплой гамме, холст на подрамнике; 1200×900 мм; центр на 1550 мм от пола | | | аналог по характеристикам | шт. | 1 | 6 | пом. 4; крепление: анкер, 2 шт. |
| ДК7 | Растение в кашпо; 450×450 мм | | | аналог по характеристикам | шт. | 1 | | пом. 4 |
| ДК8 | Ваза керамическая с ветками на обеденном столе; 200×350 мм; на M_21 | | | аналог по характеристикам | шт. | 1 | | пом. 4 |
| ДК2 | Картина над кроватью: графика в паспарту, рама — дуб; 600×700 мм; низ на 1200 мм от пола | | | аналог по характеристикам | шт. | 1 | 4 | пом. 6; крепление к стене |
| ДК5 | Зеркало в рост в тонкой чёрной раме; рама — чёрный матовый; 600×1600 мм; низ на 300 мм от пола | | | аналог по характеристикам | шт. | 1 | 12 | пом. 6; крепление: анкер для пустотелых оснований, 4 шт. |
| ДК10 | Зеркало над умывальниками, влагостойкое, в тонкой латунной раме; 1400×700 мм; низ на 1200 мм от пола | | | аналог по характеристикам | шт. | 1 | 12 | пом. 7; крепление: клей для зеркал + 2 опорных уголка снизу, анкеры по основанию |
| ДК9 | Зеркало; рама — чёрный матовый; 800×1800 мм; низ на 550 мм от пола | | | аналог по характеристикам | шт. | 1 | 18 | пом. 8; крепление: анкер, 4 шт. |
| ДК11 | Зеркало над умывальником, влагостойкое, в тонкой латунной раме; 500×700 мм; низ на 1200 мм от пола | | | аналог по характеристикам | шт. | 1 | 5 | пом. 9; крепление: клей для зеркал + 2 опорных уголка снизу |



| | | | | | | | |
|---|---|---|---|---|---|---|---|
| | | | | | Проект: Квартира с кабинетом | | |
| | Лист | № док. | Подпись | Дата | Спецификация мебели и оборудования (продолжение) | Стадия | Лист | Листов |
| Дизайнер | Кырлан А.С. | | | 04.11.26 | | П | 40 | 127 |

## Ведомость изделий

| Марка | Наименование | Пом. | Ш×Г×В, мм | Корпус | Фасад | Кромка, мм | Кол. |
|---|---|---|---|---|---|---|---|
| M_06 | Система хранения | 2 | 2200×600×2400 | ЛДСП 16 | без фасадов | 0,4 / 2 | 1 |
| M_07 | Система хранения | 2 | 1500×550×2400 | ЛДСП 16 | без фасадов | 0,4 / 2 | 1 |
| M_08 | Шкаф распашной | 3 | 2550×600×2400 | ЛДСП 16 | МДФ 18 мм, эмаль матовая; арочная фрезеровка филёнки (полукруглый верх, поле 100 мм) | 0,4 / 2 | 1 |
| M_24 | ТВ-стена | 4 | 1800×400×2500 | оцинкованный профиль ПП 60×27 / ПН 28×27 (НГ), на стене Б | панели МДФ 19 мм с волнистым рельефом, эмаль матовая | 0,4 / 2 | 1 |
| M_25 | Шкаф распашной | 4 | 3500×500×2400 | ЛДСП 16 | МДФ 18 мм, эмаль матовая | 0,4 / 2 | 1 |
| M_26 | Шкаф распашной | 6 | 1400×600×2400 | ЛДСП 16 | МДФ 18 мм, эмаль матовая | 0,4 / 2 | 1 |
| M_29 | Тумба под раковину | 7 | 1500×500×700 | ЛДСП 16 | МДФ 18 мм, эмаль матовая | 0,4 / 2 | 1 |
| M_30 | Шкаф-купе | 8 | 2000×600×2500 | ЛДСП 16 | МДФ 10 мм, эмаль матовая в профиле: алюминий, латунь матовая; вставка — зеркало серебро 4 мм, плёнка безопасности, арочная (полукруглый верх, поле 100 мм) | 0,4 / 2 | 1 |
| M_15 | Модуль нижний: мойка | 4 | 800×600×900 | ЛДСП 16 | МДФ 18 мм, эмаль матовая | 0,4 / 2 | 1 |
| M_16 | Модуль под ПММ 60: без корпуса, фасад на дверь машины | 4 | 600×600×900 | без корпуса | МДФ 18 мм, эмаль матовая — на дверь машины (навеска из её комплекта), цоколь | | 1 |
| M_17 | Модуль нижний: ящики | 4 | 600×600×900 | ЛДСП 16 | МДФ 18 мм, эмаль матовая | 0,4 / 2 | 1 |
| M_18 | Пенал: духовой шкаф, СВЧ | 4 | 600×600×2100 | ЛДСП 16 | МДФ 18 мм, эмаль матовая | 0,4 / 2 | 1 |
| M_14 | Пенал: холодильник встр. | 4 | 600×650×2100 | ЛДСП 16 | МДФ 18 мм, эмаль матовая | 0,4 / 2 | 1 |
| M_19 | Остров (M_19.1, M_19.2, M_19.3) | 4 | 1400×900×900 | ЛДСП 16 | МДФ 18 мм, эмаль матовая | 0,4 / 2 | 1 |
| M_20 | банкетка-диван вдоль окон, бархат — экран радиатора, изготовление на заказ РО-6: решётка в лицевой панели, щель 60, зазор 50 | 4 | 3200×600×850 | по чертежу | решётка по ширине прибора | 0,4 / 2 | 1 |

## Ведомость встраиваемой техники

| Поз. | Прибор | Ниша, вырез, мм | Вентиляция | Питание | Схема |
|---|---|---|---|---|---|
| M_15 | Мойка врезная / подстольная с сифоном | вырез по шаблону, ориентир 700 × 480 | | смеситель — выводы ВК | по модели |
| M_16 | Посудомоечная машина встраиваемая, 60 см | ниша 600 × 862 (от пола до низа столешницы) | зазор в цоколе, по схеме | Р32: M_17, H=300 — в соседнем модуле, за ящиком | по модели |
| M_18 | Духовой шкаф встраиваемый, 60 см | ниша 568 × 600, глубина ≥ 550; низ +820 | зазор 50 за прибором, без задней стенки; щель 50 в полке | ЭВ2: M_18, H=150 — за ящиком под нишей, доступ через ящик | по модели |
| M_18 | СВЧ-печь встраиваемая, 38 см | ниша 568 × 380, глубина ≥ 550; низ +1436 | зазор 50 за прибором, без задней стенки; щель 50 в полке | Р43: M_18, H=1960 — над нишами техники, за съёмной панелью антресоли | по модели |
| M_14 | Холодильник встраиваемый, ниша 1780 | ниша 1780 × 560 × 550 | решётка в цоколе, канал за корпусом, выход сверху | Р25: M_14, H=2000 — над нишей холодильника, съёмная панель | по модели |
| M_19.2 | Варочная панель индукционная, 60 см | вырез в столешнице 560 × 490, кромка выреза в 60 от рабочего края | зазор 40 мм под корпусом панели над верхним ящиком | ЭВ1: вывод из пола под островом, в цоколе, 700 мм от левого торца, 450 мм от рабочего края | по модели |

## Ведомость фурнитуры

| № | Фурнитура | Тип, размер | Изделия | Кол. |
|---|---|---|---|---|
| 1 | Полкодержатель с фиксацией | ø5 мм | M_06, M_07, M_08, M_25, M_26, M_29, M_30, M_18, M_14, M_19 | 236 |
| 2 | Штанга овальная 30×15, L = 712 | + 2 держателя | M_06 | 3 |
| 3 | Опора регулируемая с цоколем на клипсах | ход 20 мм | M_06, M_07, M_08, M_25, M_26, M_29, M_30 | 56 |
| 4 | Анкер по основанию стены | по таблице крепежа | M_06, M_07, M_08, M_24, M_25, M_26, M_29, M_30 | 52 |
| 5 | Уголок крепления к стене от опрокидывания | стальной | M_06, M_07, M_08, M_24, M_25, M_26, M_29, M_30, M_18, M_14 | 20 |
| 6 | Штанга овальная 30×15, L = 726 | + 2 держателя | M_07 | 1 |
| 7 | Петля накладная 110° с доводчиком | чашка 35 мм | M_08, M_25, M_26, M_29, M_15, M_18, M_14 | 109 |
| 8 | Штанга овальная 30×15, L = 996 | + 2 держателя | M_08 | 2 |
| 9 | Штанга овальная 30×15, L = 486 | + 2 держателя | M_08 | 1 |
| 10 | Штанга выдвижная торцевая | L по глубине | M_25 | 2 |
| 11 | Штанга овальная 30×15, L = 909 | + 2 держателя | M_26 | 1 |
| 12 | Система дверей купе: профиль, направляющие, ролики | на 3 двери | M_30 | 1 |
| 13 | Ручка-профиль вертикальная | в цвет профиля | M_30 | 3 |
| 14 | Штанга овальная 30×15, L = 653 | + 2 держателя | M_30 | 3 |
| 15 | Полка для обуви выдвижная наклонная | ширина 630 | M_30 | 2 |
| 16 | Полка для обуви выдвижная наклонная | ширина 653 | M_30 | 1 |
| 17 | Ручка-профиль | латунь матовая | M_15, M_16, M_17, M_18, M_14, M_19 | 21 |
| 18 | Опора кухонная регулируемая 100–120 мм | + клипса цоколя | M_15, M_17, M_18, M_14, M_19 | 30 |
| 19 | Комплект навески фасада ПММ | из поставки машины | M_16 | 1 |
| 20 | Направляющие полного выдвижения с доводчиком NL 500 | пара | M_17, M_18, M_19 | 14 |
| 21 | Уголок крепления острова к полу | стальной, в цоколе | M_19 | 4 |


## Примечания

1. Модели техники выбирает заказчик до изготовления мебели; ниши, вырезы и вентиляция — по монтажной схеме выбранной модели (условие гарантии), её номер вносится в ведомость.
2. Количество фурнитуры — по чертежам изделий; запас крепежа 5 %. Аналоги — по характеристикам (доводчик, нагрузка, ход).
3. Цвет корпусов, фасадов и профилей — по колерной карте проекта. Кромка — скрытые / видимые торцы, мм.


| | | | | | |
|---|---|---|---|---|---|
| | | | | | Проект: Квартира с кабинетом |
| | Лист | № док. | Подпись | Дата | |
| Дизайнер | Кырлан А.С. | | | 04.11.26 | Ведомости изделий, техники и фурнитуры |

| Стадия | Лист | Листов |
|---|---|---|
| П | 41 | 127 |


### Фрагмент 1. Ванная (пом. 7)

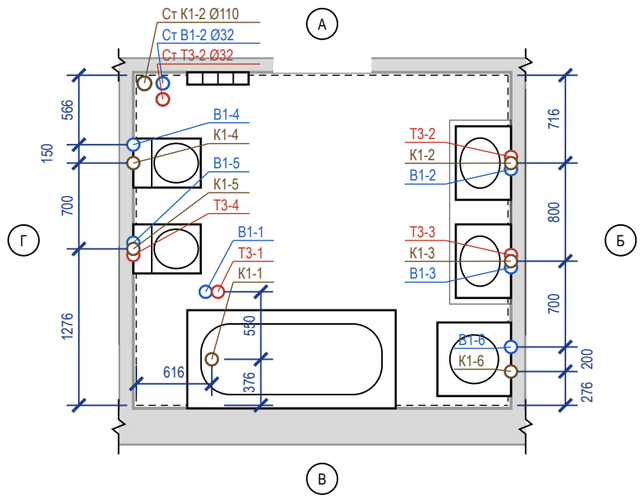


### Фрагмент 2. Санузел гостевой (пом. 9)

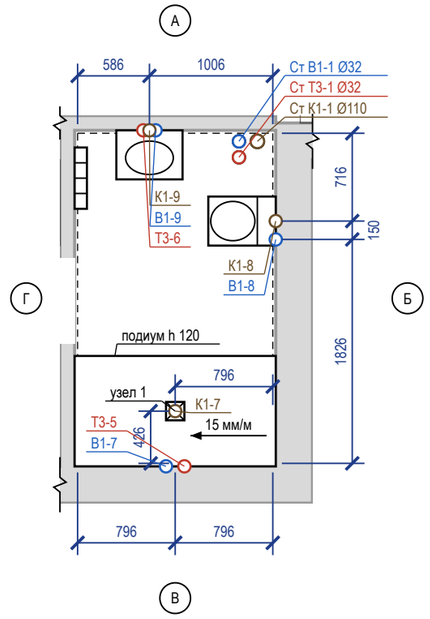


### Фрагмент 3. Кухня-гостиная (пом. 4)

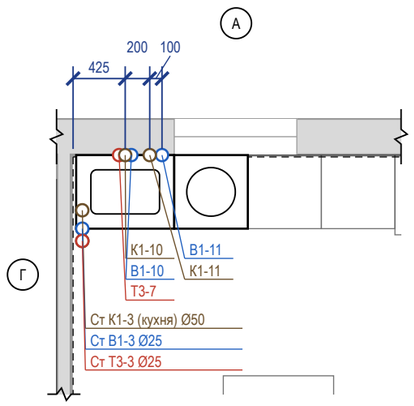


### Условные обозначения

- вывод В1 (код — в ведомости привязок)
- вывод Т3 (код — в ведомости привязок)
- вывод К1 (код — в ведомости привязок)
- сантехприбор по расстановке (габарит модели)
- чистовая поверхность стены (от неё привязки)
- стояк «Ст К1-N / Ст В1-N» (ГОСТ 21.601), Ø мм
- линия обрыва (граница фрагмента)
- трап / лоток в полу
- направление уклона К1 / пола: Ø, мм на 1 м
- А — обозначение стены А–Г (как на развёртках)

### Ведомость привязок выводов

| Код | Прибор | Ø | H, мм | Привязка от чист. стен, мм | Прим. |
|---|---|---|---|---|---|
| В1-1 | С_01 ванна | ½" | 0 | 566 от Г; 926 от В | в полу под стойку смесителя |
| Т3-1 | С_01 ванна | ½" | 0 | 666 от Г; 926 от В | в полу под стойку смесителя |
| К1-1 | С_01 ванна | Ø50 | 0 | 616 от Г; 376 от В | выпуск ванны в пол |
| В1-2 | С_02 умывальник | ½" | 550 | ст. Б: 766 от А | межос. 100 |
| Т3-2 | С_02 умывальник | ½" | 550 | ст. Б: 666 от А | межос. 100 |
| К1-2 | С_02 умывальник | Ø50 | 500 | ст. Б: 716 от А | |
| В1-3 | С_03 умывальник | ½" | 550 | ст. Б: 1126 от В | межос. 100 |
| Т3-3 | С_03 умывальник | ½" | 550 | ст. Б: 1226 от В | межос. 100 |
| К1-3 | С_03 умывальник | Ø50 | 500 | ст. Б: 1176 от В | |
| В1-4 | С_04 унитаз подвесной | ½" | 1000 | ст. Г: 566 от А | в раме инсталляции |
| К1-4 | С_04 унитаз подвесной | Ø110 | 220 | ст. Г: 716 от А | |
| В1-5 | С_05 биде подвесное | ½" | 200 | ст. Г: 1326 от В | межос. 100, в раме |
| Т3-4 | С_05 биде подвесное | ½" | 200 | ст. Г: 1226 от В | межос. 100, в раме |
| К1-5 | С_05 биде подвесное | Ø50 | 200 | ст. Г: 1276 от В | |
| В1-6 | ОБ_03 стиральная машина | ½" | 800 | ст. Б: 476 от В | кран машины |
| К1-6 | ОБ_03 стиральная машина | Ø50 | 600 | ст. Б: 276 от В | |
| В1-7 | С_07 душ | ½" | 1220 | ст. В: 721 от Г | межос. 150; 1100 от пола душа (подиум 120, +0,105) |
| Т3-5 | С_07 душ | ½" | 1220 | ст. В: 721 от Б | межос. 150; 1100 от пола душа (подиум 120, +0,105) |
| К1-7 | С_07 душ | Ø50 | 120 | 796 от Б; 426 от В | трап в подиуме 120 |
| В1-8 | С_08 унитаз подвесной | ½" | 1000 | ст. Б: 866 от А | в раме инсталляции |
| К1-8 | С_08 унитаз подвесной | Ø110 | 220 | ст. Б: 716 от А | |
| В1-9 | С_09 умывальник | ½" | 550 | ст. А: 636 от Г | межос. 100 |
| Т3-6 | С_09 умывальник | ½" | 550 | ст. А: 536 от Г | межос. 100 |
| К1-9 | С_09 умывальник | Ø50 | 500 | ст. А: 586 от Г | |
| В1-10 | М_15 мойка кухонная | ½" | 600 | ст. А: 475 от Г | межос. 100 |
| Т3-7 | М_15 мойка кухонная | ½" | 600 | ст. А: 375 от Г | межос. 100 |
| К1-10 | М_15 мойка кухонная | Ø50 | 400 | ст. А: 425 от Г | |
| В1-11 | М_16 посудомоечная машина | ½" | 550 | ст. А: 725 от Г | кран ПММ в шкафу мойки |
| К1-11 | М_16 посудомоечная машина | Ø40 | 550 | ст. А: 625 от Г | слив ПММ в шкафу мойки |


### Примечания

1. Привязки выводов даны от чистовых поверхностей стен (облицовка на сторону: ванная — 24 мм (штукатурка 10 + клей 5 + плитка 9); санузел гостевой 24 мм (штукатурка 10 + клей 5 + плитка 9); кухня-гостиная — 24 мм (фартук: штукатурка 10 + клей 5 + плитка 9)); эти же грани — на развёртках и в раскладке плитки. Высоты — от чистого пола помещения.
2. До черновой разводки сверить по паспорту выбранного прибора (смеситель, инсталляция, сифон).
3. Горячая вода (Т3) — слева от холодной (В1), если смотреть на прибор. Допуск установки выводов: ±5 мм в группе, ±20 мм у отдельно стоящих.
4. Расчёт систем водоснабжения и канализации и подбор оборудования выполняет проектная организация; лист задаёт места и высоты выводов.
5. С_01 ванна (В1-1, Т3-1, К1-1) — выводы в полу: пирог пола 35 мм их не укрывает (нужно 185 мм, расчёт — профиль К1 схемы разводки); до решения заказчика (подъём пола или другой смеситель / выпуск) не выполнять.
6. С_07 душ (В1-7, Т3-5, К1-7): трап в подиуме 120 мм — верх подиума у решётки трапа +0,105, к краю поднимается уклоном 15 мм/м: ступень по открытому краю 127 мм (край показан на плане); «узел 1» — на схеме разводки; подиум — предложение, согласовать с заказчиком. Водорозетки В1-7, Т3-5 — 1100 мм от пола душа, то есть 1220 мм от чистого пола помещения: стену размечают до подиума.
7. Посудомоечная машина М_16: кран и слив — отдельными выводами в шкафу мойки (не за машиной), до машины ≤ 1500 мм.
8. Прибор М_15 мойка кухонная, М_16 посудомоечная машина взят из расстановки мебели (по шкафу с мойкой).
9. Стояки в коробах/шахтах не замоноличивать; стояк К1 в коробе — звукоизоляция стояка в коробе без жёсткого контакта с трубой; к арматуре и ревизиям — люк не меньше 300×400.


| | | | | | |
|---|---|---|---|---|---|
| | | | | | Проект: Квартира с кабинетом — М 1:50 |
| | Лист | № док. | Подпись | Дата | |
| Дизайнер | Кырлан А.С. | | | 04.11.26 | План выводов сантехники |
| | | | | | Стадия: П; Лист: 42; Листов: 127 |

выпуск 04.11.2026 № 627e1ac6ce · стр. 42 из 127


## План квартиры (М 1:400)

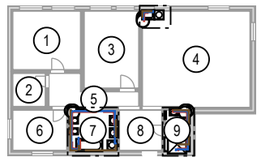



### Фр. 1. Ванная (М 1:40)

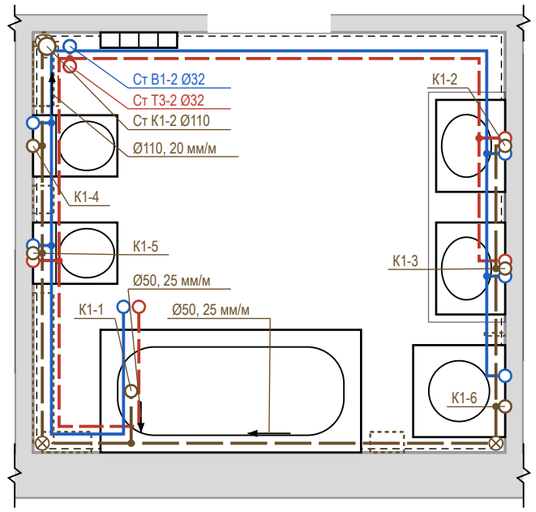



### Фр. 2. Санузел гостевой (М 1:40)

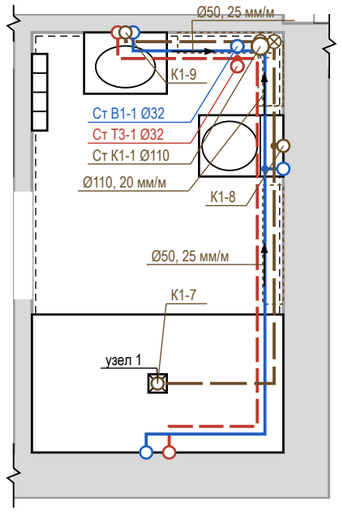


### Фр. 3. Кухня-гостиная (М 1:40)

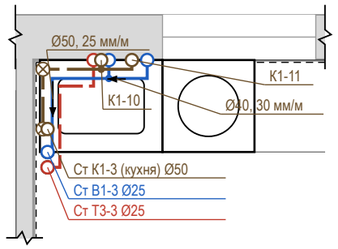


### Узел 1. Душ без поддона, трап (С_07)

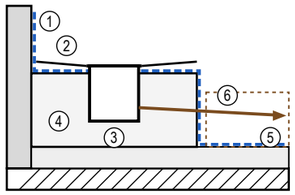


1 гидроизоляция 2 сл. на всю высоту стен душа, по всему санузлу; лента у фланца трапа и в углах
2 плитка, уклон 15 мм/м к трапу (СП 30.13330.2020, п. 17.9)
3 трап с фланцем под гидроизоляцию: монтажная высота 90 мм (до решётки) (принята, по паспорту модели)
4 подиум 120 мм у трапа, ступень 127 мм (ЦПС по гидроизоляции плиты) — предложение, согласовать с заказчиком
5 стяжка 35 мм
6 К1 Ø50, i = 25 мм/м, L = 3,11 м, Δh = 78 мм → Ст К1-1; за подиумом — короб 160×110

**Пирог ≥ 168 мм = трап 90 + Δh 78 ≤ 35 + подиум 120 + плитка 14 мм**

## Условные обозначения


- В1 — водопровод хозяйственно-питьевой (ХВС), PP-R Ø20
- Т3 — горячее водоснабжение, подача (ГВС), PP-R Ø20
- К1 — канализация бытовая
- направление уклона К1 / пола: Ø, мм на 1 м
- ⊗ ревизия (прочистка) К1 — доступ сохранить
- ● тройник (ответвление к прибору)
- короб К1 над чистым полом (ГКЛВ под плитку)
- ○ вывод В1 (код — в ведомости привязок)
- ○ вывод Т3 (код — в ведомости привязок)
- ○ вывод К1 (код — в ведомости привязок)
- сантехприбор по расстановке (габарит модели)
- ○ стояк «Ст К1-N / Ст В1-N» (ГОСТ 21.601), Ø мм
- линия обрыва (граница фрагмента)
- граница фрагмента на плане (Фр. N)

## Профиль выпусков К1 (до врезки в стояк)

| Выпуск | Прибор | Ø | L, м | i, мм/м | Δh, мм | Прокладка, мм |
|---|---|---|---|---|---|---|
| К1-8 | С_08 унитаз подвесной | Ø110 | 0,86 | 20 | 17 | короб 160×140 |
| К1-4 | С_04 унитаз подвесной | Ø110 | 0,80 | 20 | 16 | короб 160×140 |
| К1-2 | С_02 умывальник | Ø50 | 7,64 | 25 | 191 | короб 280×110 |
| К1-3 | С_03 умывальник | Ø50 | 6,84 | 25 | 171 | короб 260×110 |
| К1-6 | ОБ_03 стиральная машина | Ø50 | 5,94 | 25 | 149 | короб 230×110 |
| К1-1 | С_01 ванна | Ø50 | 3,60 | 25 | 90 | в полу не помещается: 185 > 35; до решения |
| К1-7 | С_07 душ | Ø50 | 3,11 | 25 | 78 | трап в подиуме 120 (35 + 120 + 14 ≥ 168), далее короб 160×110 |
| К1-5 | С_05 биде подвесное | Ø50 | 1,50 | 25 | 38 | короб 120×110 |
| К1-9 | С_09 умывальник | Ø50 | 0,97 | 25 | 24 | короб 110×110 |
| К1-10 | М_15 мойка кухонная | Ø50 | 0,86 | 25 | 22 | над полом за приборами |
| К1-11 | М_16 посудомоечная машина | Ø40 | 1,06 | 30 | 32 | над полом за приборами |

Короб h×b: h — от чистого пола, b — от чистовой стены. Стяжка 35 мм — лист полов.

## Узел ввода В1, Т3 (по данным, без масштаба)

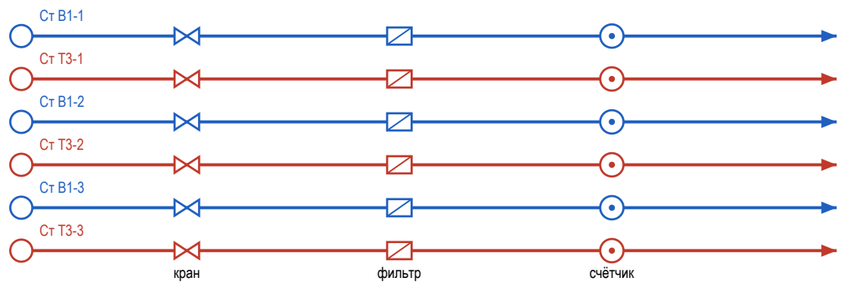


⊗ Ст К1-1, Ст К1-2, Ст К1-3 (кухня): ревизия на стояке — люк в коробе


## Примечания

1. Трассы принципиальные, построены от стояков вдоль стен помещений; фактическое положение фиксируется исполнительной схемой с привязками (фото с рулеткой) до закрытия.
2. Уклон К1 не менее 1/d и не более 150 мм/м (СП 30.13330.2020, п. 19.1), приняты практические уклоны; поворот — двумя отводами 45°, ревизия после поворота, доступ сохранить. Стояк К1 в коробе — звукоизоляция стояка в коробе, без жёсткого контакта короба с трубой.
3. Решение по К1: стяжка 35 мм не укрывает трубы (нужно Ø + Δh + 45 мм) — выпуски идут над чистым полом вдоль стен: К1-10, К1-11 — за приборами и в раме инсталляции; К1-8, К1-4, К1-2, К1-3, К1-6, К1-5, К1-9 — в коробе ГКЛВ под плитку (размеры в профиле). Короба — на развёртках; отметку низа врезки в стояк замерить до черновых работ.
4. К1-7 (С_07 душ, трап): монтажная высота трапа 90 до верха решётки (по паспорту) + уклон 78 = 168 мм ≤ стяжка 35 + подиум 120 + облицовка 14 мм трап в подиуме душевой зоны (узел 1 на этом листе), за краем подиума отвод — в коробе ГКЛВ 160×110 вдоль стены; подиум — предложение, согласовать с заказчиком.
5. К1-1 (С_01 ванна, выпуск в пол): Δh 90 + Ø50 + 45 = 185 мм > пирога 35 мм — в стяжке не помещается, в короб не уходит: подиум или подъём пола на 150 мм или прибор ближе к стояку — решение заказчика; до решения не выполнять.
6. Отводы К1-2 (7,6 м), К1-3 (6,8 м), К1-6 (5,9 м) длиннее 4 м без вентиляции — у прибора воздушный клапан Ø50 в доступном месте (за люком или в тумбе) либо вентилируемый отвод (EN 12056-2, табл. 4), подбор — проектная организация.
7. Узел ввода В1, Т3 — по данным проекта: кран → фильтр → счётчик. Доступ к арматуре — через люк не меньше 300×400. Водопровод — в штробе стен или в коробах; трубы испытать давлением до закрытия (акт скрытых работ).
8. Расчёт систем, диаметры магистралей и подбор оборудования выполняет проектная организация; врезка и перенос стояков — по согласованию с управляющей организацией. Арматуру и привязки сверить по паспортам приборов.

| | | | | | |
|---|---|---|---|---|---|
| | | | | | Проект: Квартира с кабинетом |
| | Лист | № док. | Подпись | Дата | Схема разводки водопровода и канализации |
| Дизайнер | Кырлан А.С. | | | 04.11.26 | |

| Стадия | Лист | Листов |
|---|---|---|
| П | 43 | 127 |

## Схема В1 (М 1:50; по вертикали и горизонтали один масштаб, глубина — ×0,5 под 45°)

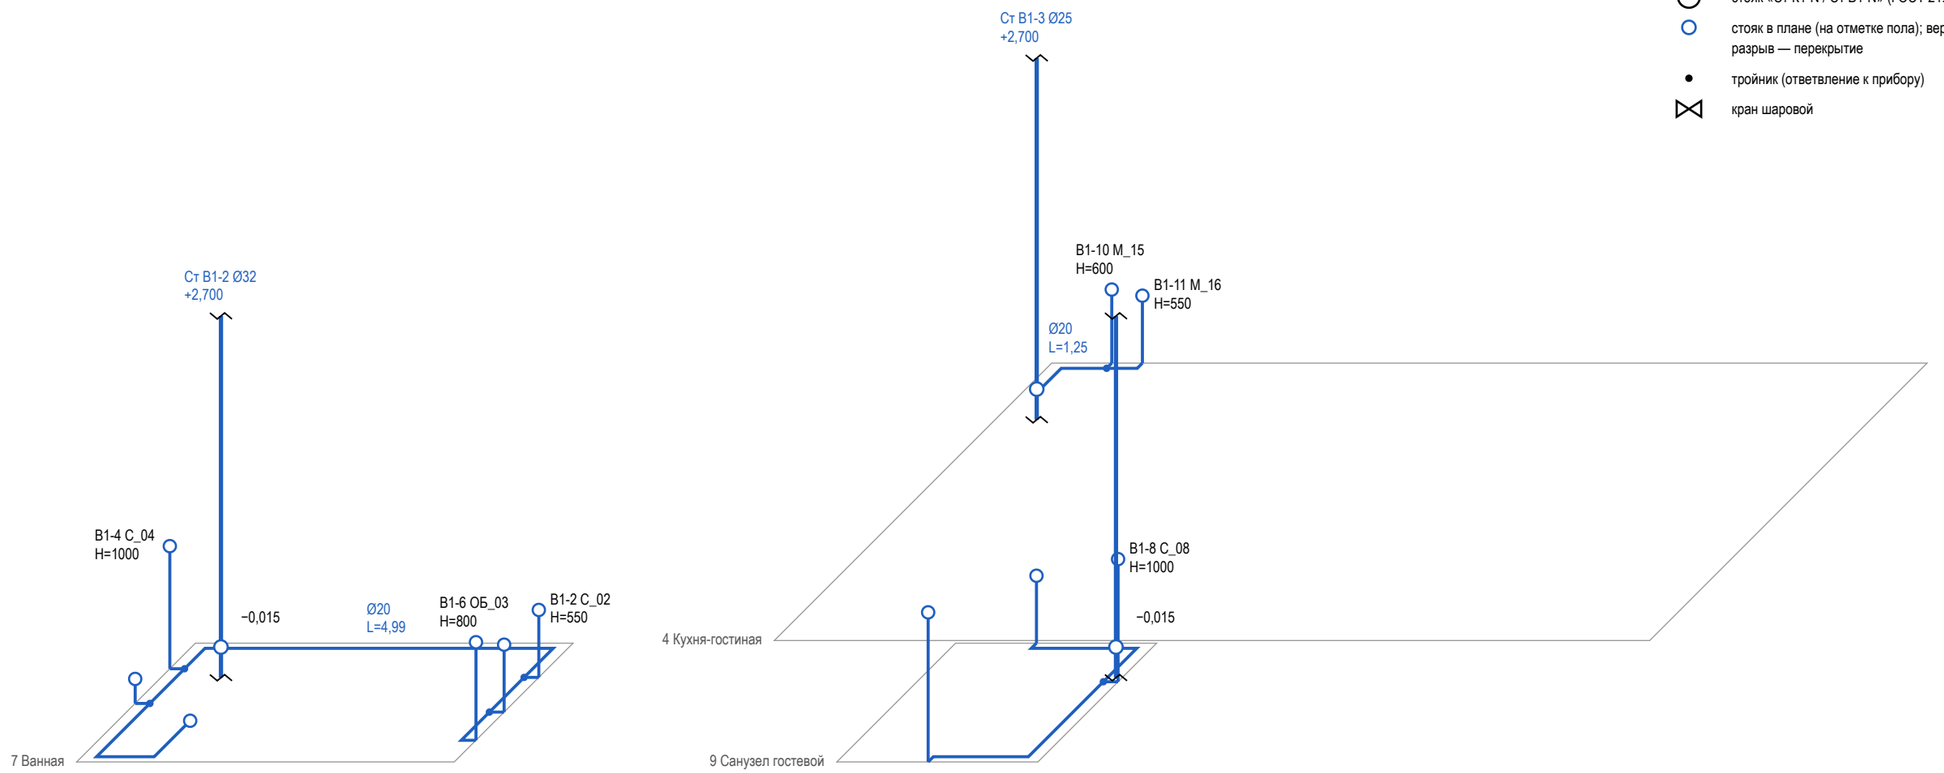


### Условные обозначения

- В1 — водопровод хозяйственно-питьевой (ХВС), PP-R Ø20
- вывод В1 (код — в ведомости привязок)
- стояк «Ст К1-N / Ст В1-N» (ГОСТ 21.601), Ø мм
- стояк в плане (на отметке пола); вертикаль — стояк по высоте, разрыв — перекрытие
- тройник (ответвление к прибору)
- кран шаровой

### Примечания


1. Схема В1 построена по тем же трассам, что план разводки: положение в плане сохранено, глубина — в масштабе ×0,5. Трассы принципиальные; фактическое положение фиксируется исполнительной схемой до закрытия.
2. Высоты Н — от чистого пола помещения, мм. Прокладка магистрали В1 по данным: в стяжке пола, в стяжке пола, выше плиты перекрытия; отметка трасс — по пирогу пола.
3. Узел ввода В1 (кран, фильтр, счётчик, обратный клапан, кран) — на схеме разводки; состав узла ввода — по согласованию. Кран шаровой — на первом участке от стояка.
4. Трубы испытать давлением до закрытия (акт скрытых работ, опрессовка по СП 73.13330.2016).
5. Диаметры, высоты выводов и места кранов — по паспортам выбранных приборов и расчёту проектной организации.
6. Расчёт систем, диаметры магистралей и подбор оборудования выполняет проектная организация.

| | | | | | | | |
|---|---|---|---|---|---|---|---|
| | | | | | Проект: Квартира с кабинетом | | М 1:50 |
| | Лист | № док. | Подпись | Дата | Аксонометрическая схема В1 (холодное водоснабжение) | Стадия | Лист | Листов |
| Дизайнер | Кырлан А.С. | | | 04.11.26 | | П | 44 | 127 |

## Схема Т3 (М 1:50; по вертикали и горизонтали один масштаб, глубина — ×0,5 под 45°)

### Условные обозначения

- Т3 — горячее водоснабжение, подача (ГВС), PP-R Ø20
- вывод Т3 (код — в ведомости привязок)
- стояк «Ст К1-N / Ст В1-N» (ГОСТ 21.601), Ø мм
- стояк в плане (на отметке пола); вертикаль — стояк по высоте, разрыв — перекрытие
- тройник (ответвление к прибору)
- кран шаровой

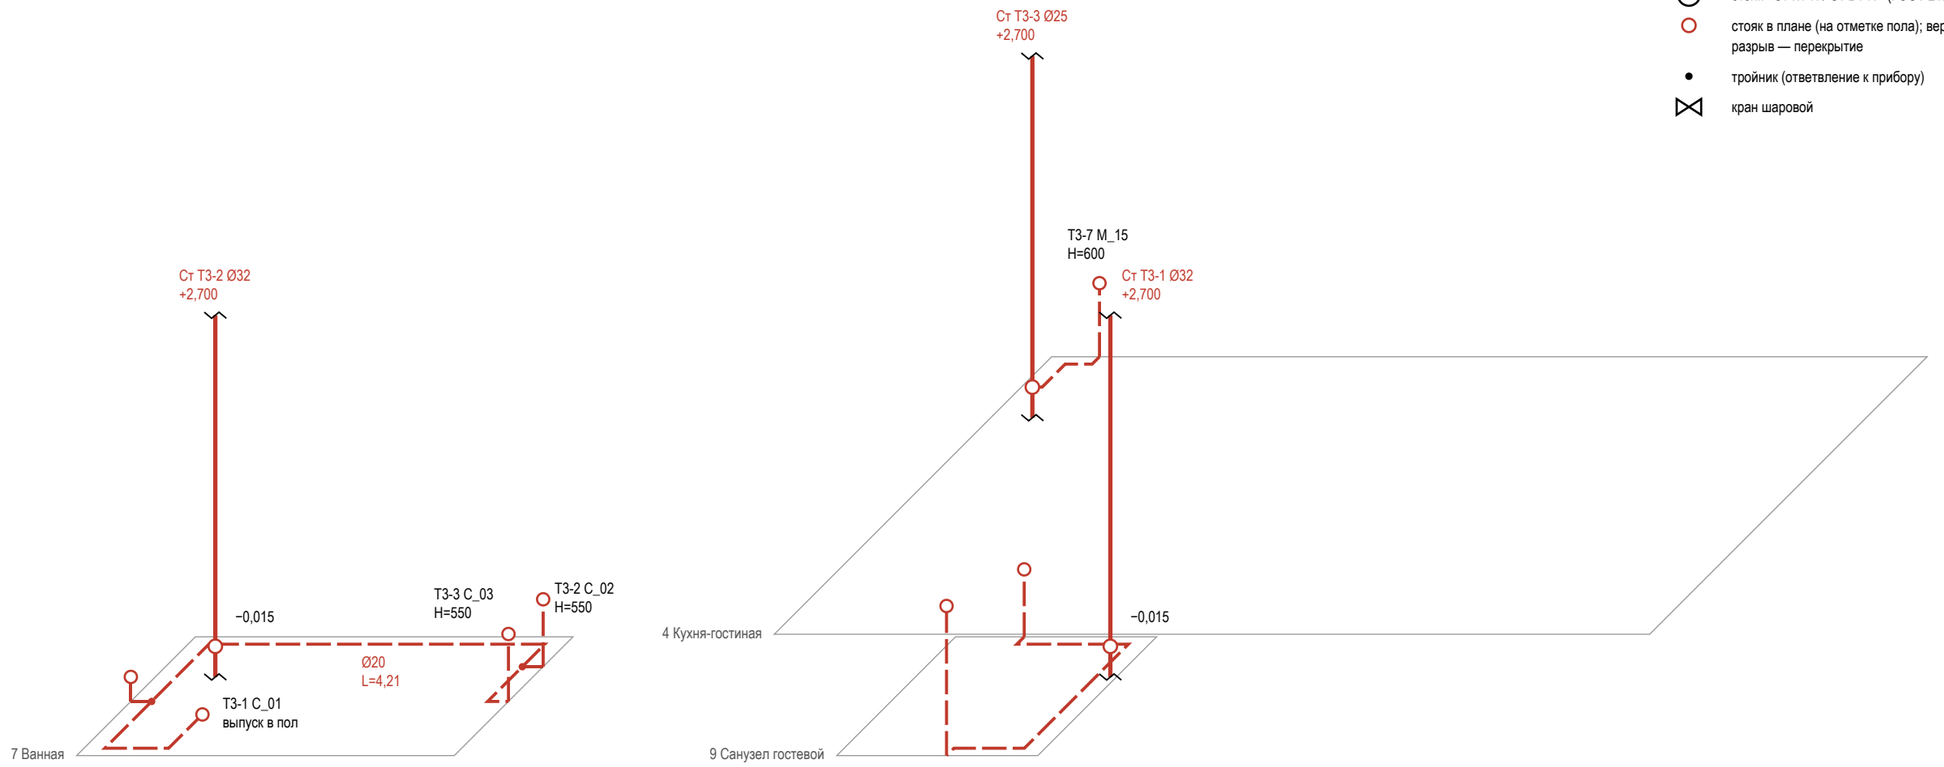



### Примечания

1. Схема Т3 построена по тем же трассам, что план разводки: положение в плане сохранено, глубина — в масштабе ×0,5. Трассы принципиальные; фактическое положение фиксируется исполнительной схемой до закрытия.
2. Высоты Н — от чистого пола помещения, мм. Прокладка магистрали Т3 по данным: в стяжке пола, в стяжке пола, выше плиты перекрытия; отметка трасс — по пирогу пола.
3. Узел ввода Т3 (кран, фильтр, счётчик, обратный клапан, кран) — на схеме разводки; состав узла ввода — по согласованию. Кран шаровой — на первом участке от стояка.
4. Циркуляция ГВС в данных не задана — циркуляционного трубопровода на схеме нет.
5. Трубы испытать давлением до закрытия (акт скрытых работ, опрессовка по СП 73.13330.2016).
6. Диаметры, высоты выводов и места кранов — по паспортам выбранных приборов и расчёту проектной организации.
7. Расчёт систем, диаметры магистралей и подбор оборудования выполняет проектная организация.

| | | | | | | |
|---|---|---|---|---|---|---|
| | | | | | Проект: Квартира с кабинетом | **М 1:50** |
| | Лист | № док. | Подпись | Дата | Аксонометрическая схема Т3 (горячее водоснабжение) | Стадия / Лист / Листов |
| Дизайнер | Кырлан А.С. | | | 04.11.26 | | П / 45 / 127 |

## Схема К1 (М 1:50; по вертикали и горизонтали один масштаб, глубина — ×0,5 под 45°)

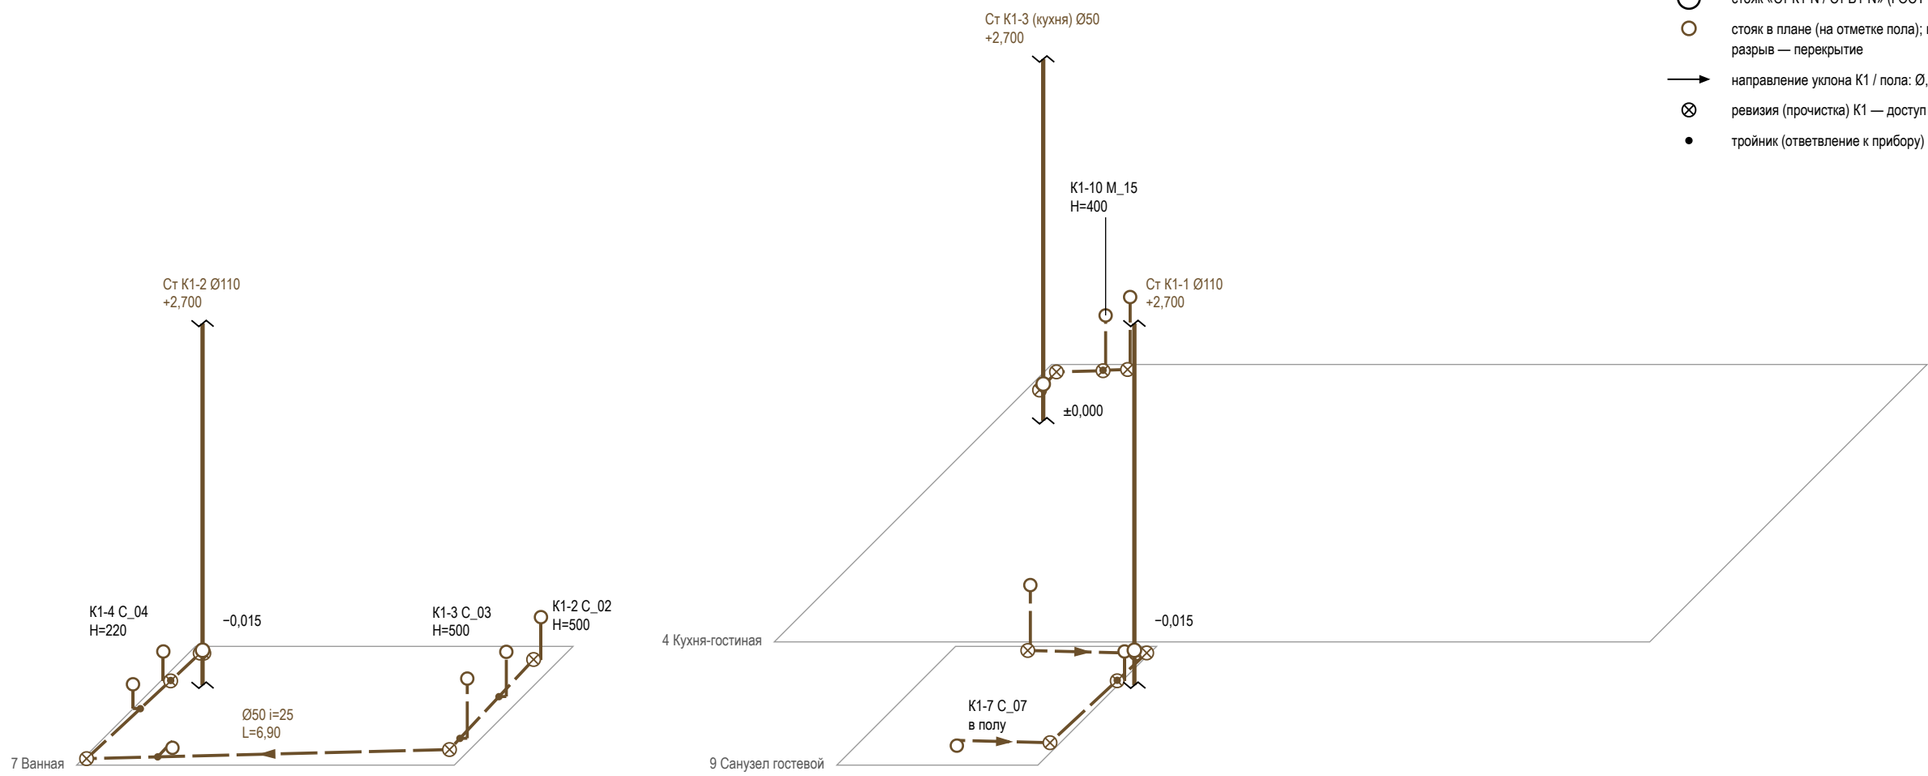


### Условные обозначения


- К1 — канализация бытовая
- вывод К1 (код — в ведомости привязок)
- стояк «Ст К1-N / Ст В1-N» (ГОСТ 21.601), Ø мм
- стояк в плане (на отметке пола); вертикаль — стояк по высоте, разрыв — перекрытие
- направление уклона К1 / пола: Ø, мм на 1 м
- ревизия (прочистка) К1 — доступ сохранить
- тройник (ответвление к прибору)

### Примечания

1. Схема К1 построена по тем же трассам, что план разводки: положение в плане сохранено, глубина — в масштабе ×0,5. Трассы принципиальные; фактическое положение фиксируется исполнительной схемой до закрытия.
2. Отметки — от плиты перекрытия: низ трубы у врезки в стояк — отметка из данных выпуска, к прибору труба поднимается на уклон i, мм/м (уклон не менее 1/d и не более 150 мм/м, СП 30.13330.2020, п. 19.1); чистый пол — выше плиты на стяжку (высота пирога пола). Высота выпуска прибора Н — от чистого пола.
3. Ревизия — на повороте и в начале участка; стояк К1 в коробе с люком — звукоизоляция стояка в коробе; поворот — двумя отводами 45°.
4. Трубы испытать давлением до закрытия (акт скрытых работ, опрессовка по СП 73.13330.2016).
5. Диаметры, высоты выводов и места кранов — по паспортам выбранных приборов и расчёту проектной организации.
6. Расчёт систем, диаметры магистралей и подбор оборудования выполняет проектная организация.

| | | | | | | |
|---|---|---|---|---|---|---|
| | | | | | Проект: Квартира с кабинетом | М 1:50 |
| | Лист | № док. | Подпись | Дата | | |
| Дизайнер | Кырлан А.С. | | | 04.11.26 | Аксонометрическая схема К1 (канализация) | Стадия: П; Лист: 46; Листов: 127 |

## Стена А (М 1:25)

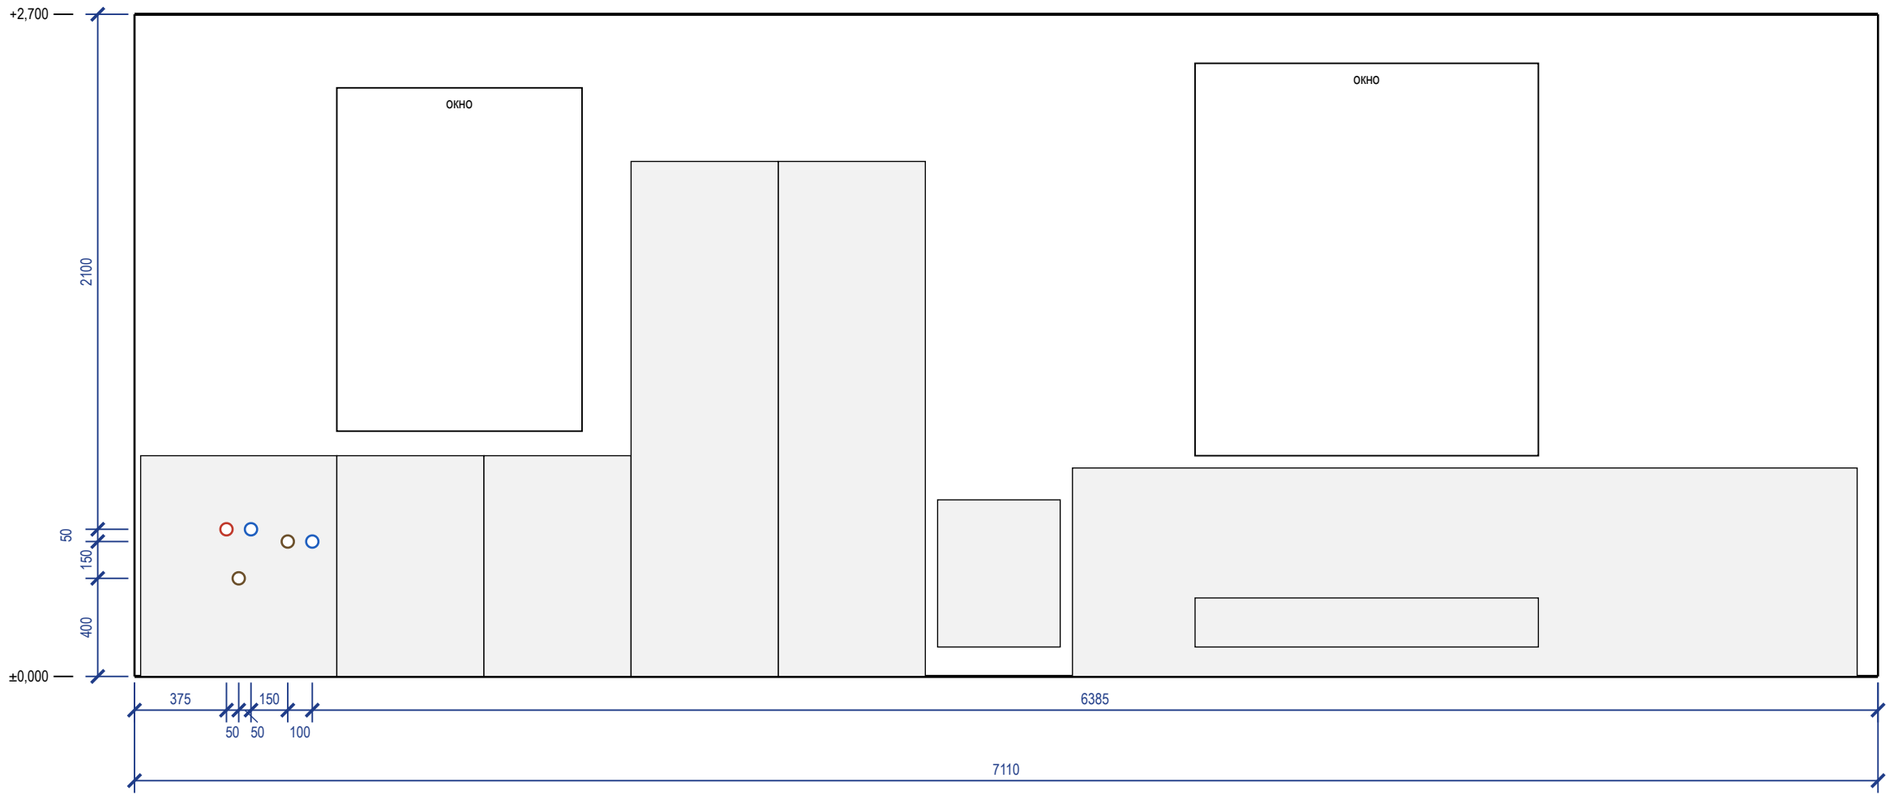


## Ведомость привязок выводов (от чистого пола и угла)

| Код | Прибор | Ø | H, мм | Привязка, мм |
|---|---|---|---|---|
| В1-10 | М_15 мойка кухонная | ½" | 600 | ст. А: 475 от лев. угла |
| Т3-7 | М_15 мойка кухонная | ½" | 600 | ст. А: 375 от лев. угла |
| К1-10 | М_15 мойка кухонная | Ø50 | 400 | ст. А: 425 от лев. угла |
| В1-11 | М_16 посудомоечная машина | ½" | 550 | ст. А: 725 от лев. угла |
| К1-11 | М_16 посудомоечная машина | Ø40 | 550 | ст. А: 625 от лев. угла |

## Условные обозначения


- вывод В1 (код — в ведомости привязок)
- вывод Т3 (код — в ведомости привязок)
- вывод К1 (код — в ведомости привязок)
- сантехприбор по расстановке (габарит модели)
- дверной проём; окно — сплошной контур

## Примечания


1. Габариты и высоты приборов, межосевые смесителей и места кранов — по паспортам выбранных приборов, сверяются до разметки стен.
2. Высоты H — от чистого пола помещения, мм; отметка чистого пола и потолка — у левого края вида (от ±0,000 объекта). Привязки — от левого чистового угла вида (облицовка стен вычтена), как на развёртках стен.
3. Стояки в помещении: Ст К1-3 (кухня) Ø50, Ст В1-3 Ø25, Ст Т3-3 Ø25 — положение на плане выводов; выводы подключаются к ним по схеме разводки.
4. Ревизионные люки (арматура и ревизии у М_15, М_16 300×400, стена А у М_15, предложение): привязка к углу — по раскладке плитки, подтверждается обмером.
5. Ревизионные люки к арматуре и ревизиям в данных не заданы: место и размер не определены (записи реестра нет).
6. Мойка, ПММ и фильтр — выводы в шкафу мойки; диаметры и положение сифона и кранов сверить по паспортам приборов и чертежам модуля.
7. Часть подписей выводов не уместилась у знака: коды и высоты — в ведомости привязок.
8. Расчёт систем водоснабжения и канализации и подбор оборудования выполняет проектная организация; лист задаёт места и высоты выводов.

| | | | | | | |
|---|---|---|---|---|---|---|
| | | | | | Проект: Квартира с кабинетом | М 1:25 |
| | Лист | № док. | Подпись | Дата | | |
| Дизайнер | Кырлан А.С. | | | 04.11.26 | Развёртки мокрых зон: выводы ВК. Кухня-гостиная | Стадия: П; Лист: 47; Листов: 127 |

### Стена А (М 1:20)

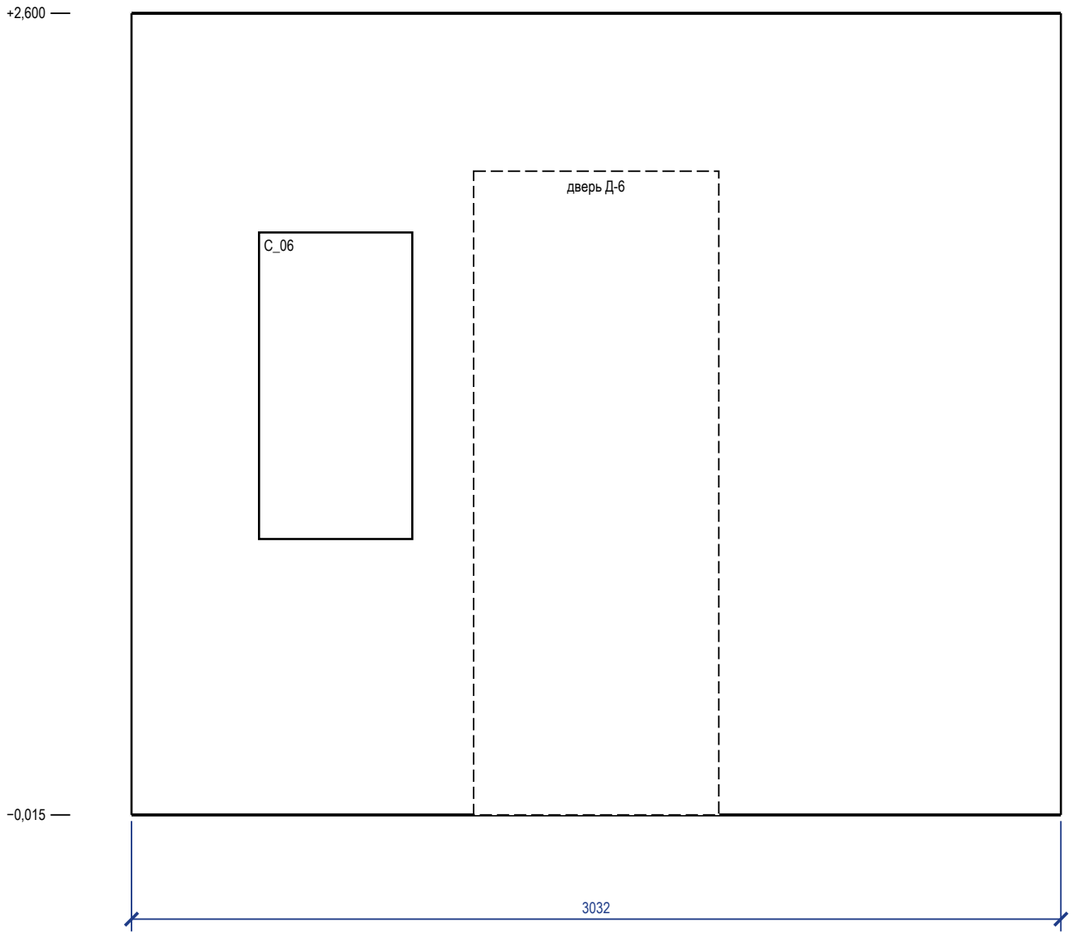


### Стена Б (М 1:20)

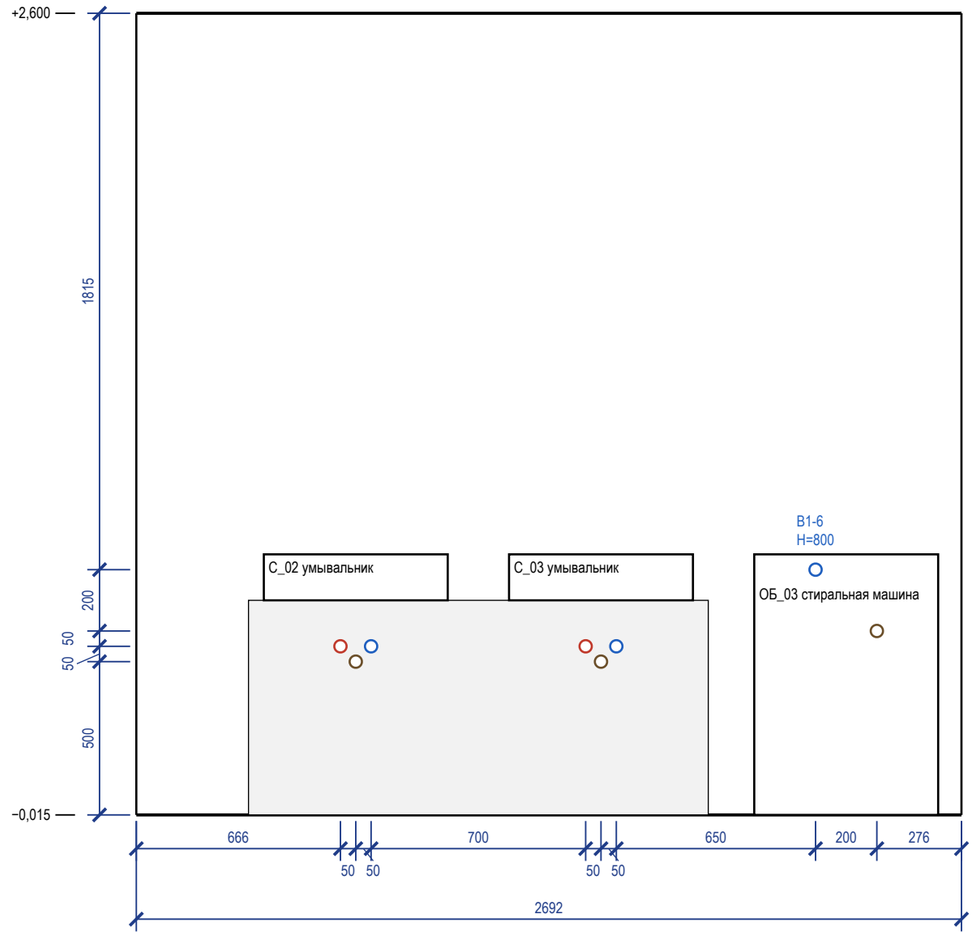


### Ведомость привязок выводов (от чистого пола и угла)

| Код | Прибор | Ø | H, мм | Привязка, мм |
|---|---|---|---|---|
| В1-2 | С_02 умывальник | ½" | 550 | ст. Б: 766 от лев. угла |
| Т3-2 | С_02 умывальник | ½" | 550 | ст. Б: 666 от лев. угла |
| К1-2 | С_02 умывальник | Ø50 | 500 | ст. Б: 716 от лев. угла |
| В1-3 | С_03 умывальник | ½" | 550 | ст. Б: 1566 от лев. угла |

### Ведомость привязок (продолжение)

| Код | Прибор | Ø | H, мм | Привязка, мм |
|---|---|---|---|---|
| Т3-3 | С_03 умывальник | ½" | 550 | ст. Б: 1466 от лев. угла |
| К1-3 | С_03 умывальник | Ø50 | 500 | ст. Б: 1516 от лев. угла |
| В1-6 | ОБ_03 стиральная машина | ½" | 800 | ст. Б: 2216 от лев. угла |
| К1-6 | ОБ_03 стиральная машина | Ø50 | 600 | ст. Б: 2416 от лев. угла |

### Условные обозначения

- вывод В1 (код — в ведомости привязок)
- вывод Т3 (код — в ведомости привязок)
- вывод К1 (код — в ведомости привязок)
- сантехприбор по расстановке (габарит модели)
- дверной проём; окно — сплошной контур


### Примечания

1. Габариты и высоты приборов, межосевые смесителей и места кранов — по паспортам выбранных приборов, сверяются до разметки стен.
2. Высоты H — от чистого пола помещения, мм; отметка чистого пола и потолка — у левого края вида (от ±0,000 объекта). Привязки — от левого чистового угла вида (облицовка стен вычтена), как на развёртках стен.
3. Выводы в полу (В1-1, Т3-1, К1-1): трап, лоток, выпуск отдельностоящей ванны, подвод к стойке напольного смесителя — на развёртке их нет; место и пирог пола — лист «Схема разводки» (профиль К1, узел 1).
4. Стояки в помещении: Ст К1-2 Ø110, Ст В1-2 Ø32, Ст Т3-2 Ø32 — положение на плане выводов; выводы подключаются к ним по схеме разводки.
5. Ревизионные люки (арматура и ревизии у С_01 300×400, стена В у С_01, предложение): привязка к углу — по раскладке плитки, подтверждается обмером.
6. Ревизионные люки к арматуре и ревизиям в данных не заданы: место и размер не определены (записи реестра нет).
7. Часть подписей выводов не уместилась у знака: коды и высоты — в ведомости привязок.
8. Помещение «Ванная» — 2 листа: стены 1) А, Б; 2) В, Г.
9. Расчёт систем водоснабжения и канализации и подбор оборудования выполняет проектная организация; лист задаёт места и высоты выводов.


| | | | | | | |
|---|---|---|---|---|---|---|
| | | | | | Проект: Квартира с кабинетом | М 1:20 |
| | Лист | № док. | Подпись | Дата | Развёртки мокрых зон: выводы ВК. Ванная (лист 1 из 2) | |
| Дизайнер | Кырлан А.С. | | | 04.11.26 | | |

| Стадия | Лист | Листов |
|---|---|---|
| П | 48 | 127 |

## Стена В (М 1:20)

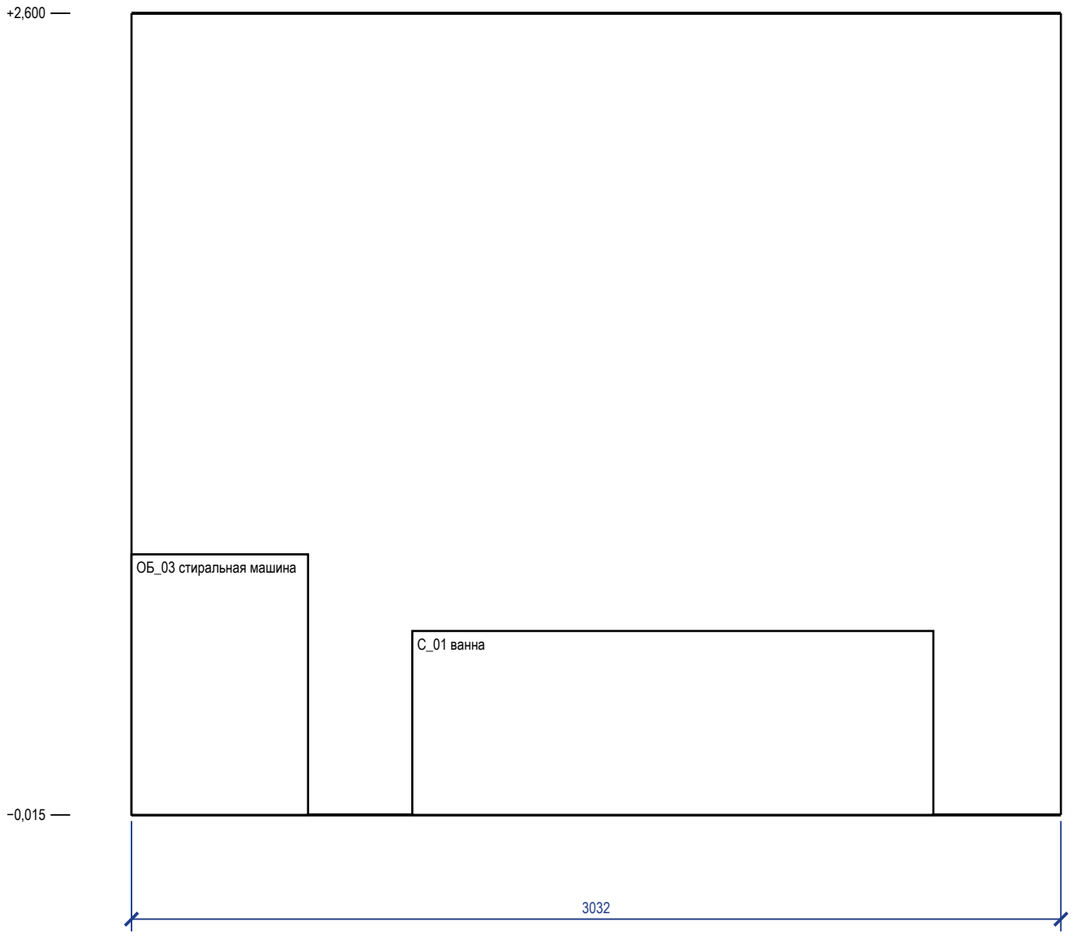


## Стена Г (М 1:20)

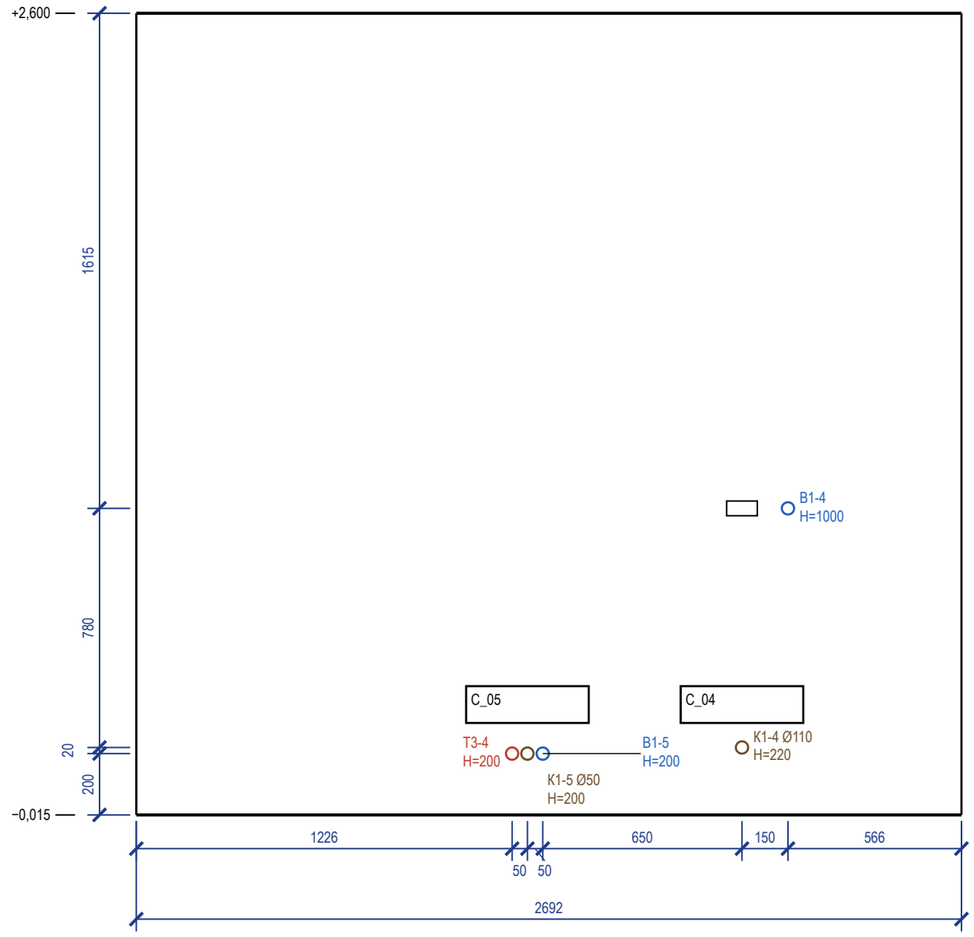


## Ведомость привязок выводов (от чистого пола и угла)

| Код | Прибор | Ø | Н, мм | Привязка, мм |
|---|---|---|---|---|
| В1-4 | С_04 унитаз подвесной | ½" | 1000 | ст. Г: 2126 от лев. угла |
| К1-4 | С_04 унитаз подвесной | Ø110 | 220 | ст. Г: 1976 от лев. угла |
| В1-5 | С_05 биде подвесное | ½" | 200 | ст. Г: 1326 от лев. угла |

## Ведомость привязок (продолжение)

| Код | Прибор | Ø | Н, мм | Привязка, мм |
|---|---|---|---|---|
| Т3-4 | С_05 биде подвесное | ½" | 200 | ст. Г: 1226 от лев. угла |
| К1-5 | С_05 биде подвесное | Ø50 | 200 | ст. Г: 1276 от лев. угла |

## Условные обозначения

- вывод В1 (код — в ведомости привязок)
- вывод Т3 (код — в ведомости привязок)
- вывод К1 (код — в ведомости привязок)
- сантехприбор по расстановке (габарит модели)
- дверной проём; окно — сплошной контур
- кнопка смыва инсталляции (Н — по данным прибора)

## Примечания

1. Габариты и высоты приборов, межосевые смесителей и места кранов — по паспортам выбранных приборов, сверяются до разметки стен.
2. Высоты Н — от чистого пола помещения, мм; отметка чистого пола и потолка — у левого края вида (от ±0,000 объекта). Привязки — от левого чистового угла вида (облицовка стен вычтена), как на развёртках стен.
3. Кнопка смыва С_04 — Н=1000 (по данным прибора).
4. Выводы в полу (В1-1, Т3-1, К1-1): трап, лоток, выпуск отдельностоящей ванны, подвод к стойке напольного смесителя — на развёртке их нет; место и пирог пола — лист «Схема разводки» (профиль К1, узел 1).
5. Стояки в помещении: Ст К1-2 Ø110, Ст В1-2 Ø32, Ст Т3-2 Ø32 — положение на плане выводов; выводы подключаются к ним по схеме разводки.
6. Ревизионные люки (арматура и ревизии у С_01 300×400, стена В у С_01, предложение): привязка к углу — по раскладке плитки, подтверждается обмером.
7. Ревизионные люки к арматуре и ревизиям в данных не заданы: место и размер не определены (записи реестра нет).
8. Помещение «Ванная» — 2 листа: стены 1) А, Б; 2) В, Г.
9. Расчёт систем водоснабжения и канализации и подбор оборудования выполняет проектная организация; лист задаёт места и высоты выводов.

| | | | | |
|---|---|---|---|---|
| | | | | |
| | Лист | № док. | Подпись | Дата |
| Дизайнер | Кырлан А.С. | | | 04.11.26 |


Проект: Квартира с кабинетом — **М 1:20**

Развёртки мокрых зон: выводы ВК. Ванная (лист 2 из 2)


| Стадия | Лист | Листов |
|---|---|---|
| П | 49 | 127 |

выпуск 04.11.2026 № 627e1ac6ce · стр. 49 из 127

### Стена А (М 1:20)

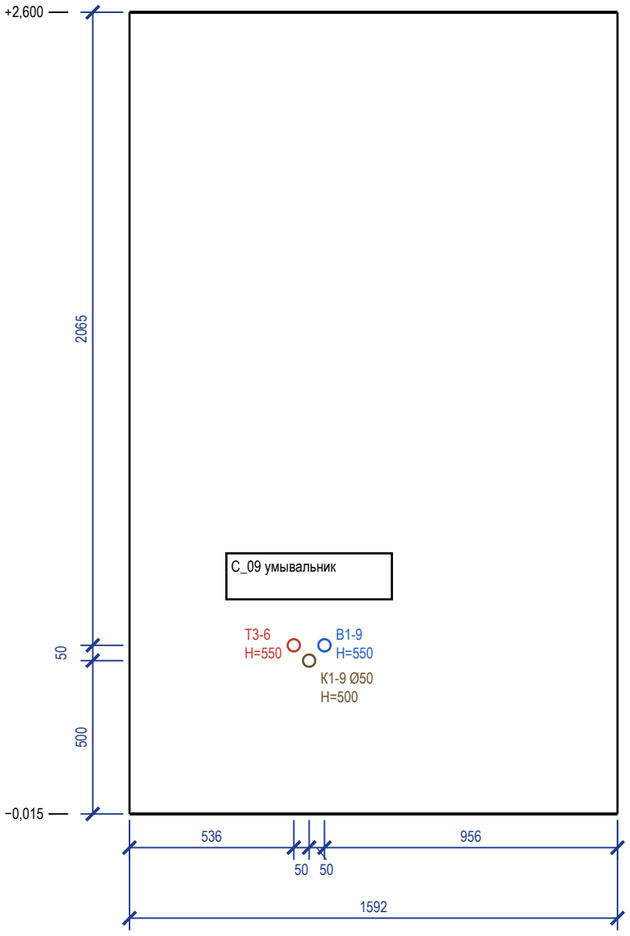


### Стена Б (М 1:20)

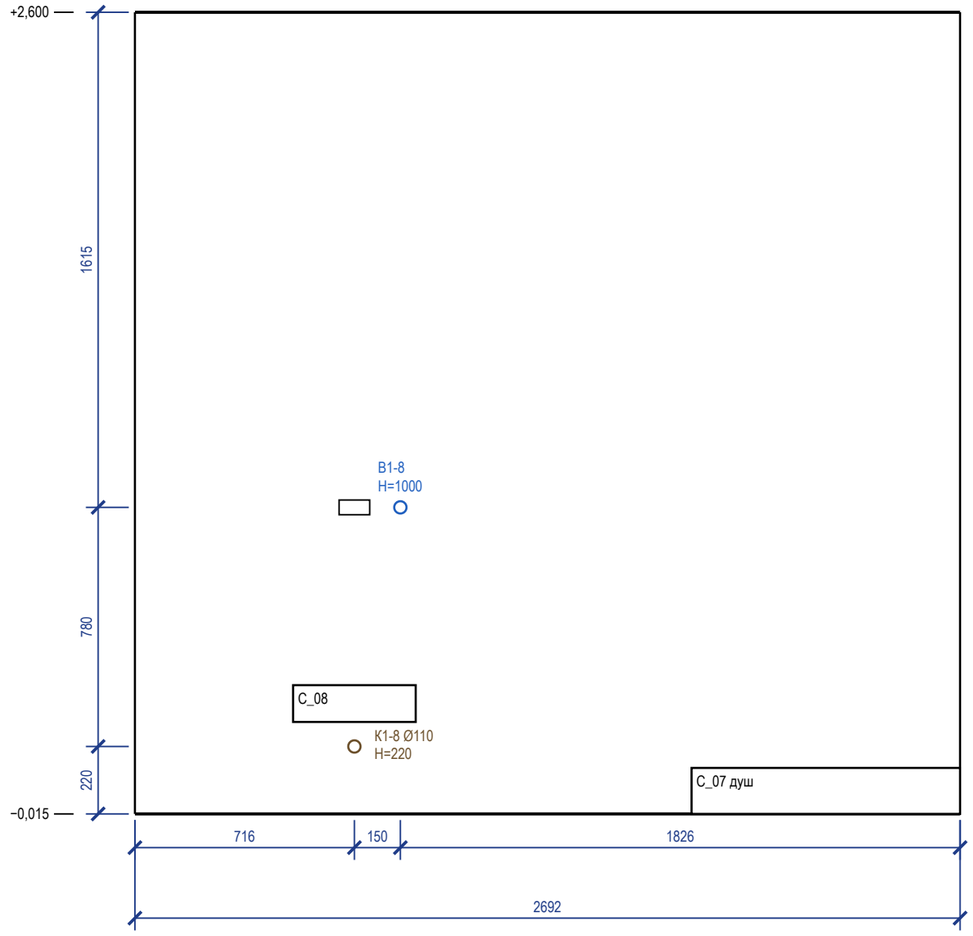


### Ведомость привязок выводов (от чистого пола и угла)

| Код | Прибор | Ø | H, мм | Привязка, мм |
|---|---|---|---|---|
| B1-9 | C_09 умывальник | ½" | 550 | ст. А: 636 от лев. угла |
| T3-6 | C_09 умывальник | ½" | 550 | ст. А: 536 от лев. угла |
| K1-9 | C_09 умывальник | Ø50 | 500 | ст. А: 586 от лев. угла |

### Ведомость привязок (продолжение)

| Код | Прибор | Ø | H, мм | Привязка, мм |
|---|---|---|---|---|
| B1-8 | C_08 унитаз подвесной | ½" | 1000 | ст. Б: 866 от лев. угла |
| K1-8 | C_08 унитаз подвесной | Ø110 | 220 | ст. Б: 716 от лев. угла |

### Условные обозначения


- вывод B1 (код — в ведомости привязок)
- вывод T3 (код — в ведомости привязок)
- вывод K1 (код — в ведомости привязок)
- сантехприбор по расстановке (габарит модели)
- дверной проём; окно — сплошной контур
- кнопка смыва инсталляции (H — по данным прибора)

### Примечания


1. Габариты и высоты приборов, межосевые смесителей и места кранов — по паспортам выбранных приборов, сверяются до разметки стен.
2. Высоты H — от чистого пола помещения, мм; отметка чистого пола и потолка — у левого края вида (от ±0,000 объекта). Привязки — от левого чистового угла вида (облицовка стен вычтена), как на развёртках стен.
3. Кнопка смыва C_08 — H=1000 (по данным прибора).
4. Выводы в полу (K1-1): трап, лоток, выпуск отдельностоящей ванны, подвод к стойке напольного смесителя — на развёртке их нет; место и пирог пола лист «Схема разводки» (профиль K1, узел 1).
5. Стояки в помещении: Ст K1-1 Ø110, Ст B1-1 Ø32, Ст T3-1 Ø32 — положение на плане выводов; выводы подключаются к ним по схеме разводки.
6. Ревизионные люки (арматура и ревизии у C_07 300×400, стена В у C_07, предложение): привязка к углу — по раскладке плитки, подтверждается обмером.
7. Ревизионные люки к арматуре и ревизиям в данных не заданы: место и размер не определены (записи реестра нет).
8. Помещение «Санузел гостевой» — 2 листа: стены 1) А, Б; 2) В, Г.
9. Расчёт систем водоснабжения и канализации и подбор оборудования выполняет проектная организация; лист задаёт места и высоты выводов.

| | | | | | |
|---|---|---|---|---|---|
| | | | | | Проект: Квартира с кабинетом — М 1:20 |
| | Лист | № док. | Подпись | Дата | Развёртки мокрых зон: выводы ВК. Санузел гостевой (лист 1 из 2) |
| Дизайнер | Кырлан А.С. | | | 04.11.26 | Стадия: П · Лист: 50 · Листов: 127 |

## Стена В (М 1:20)

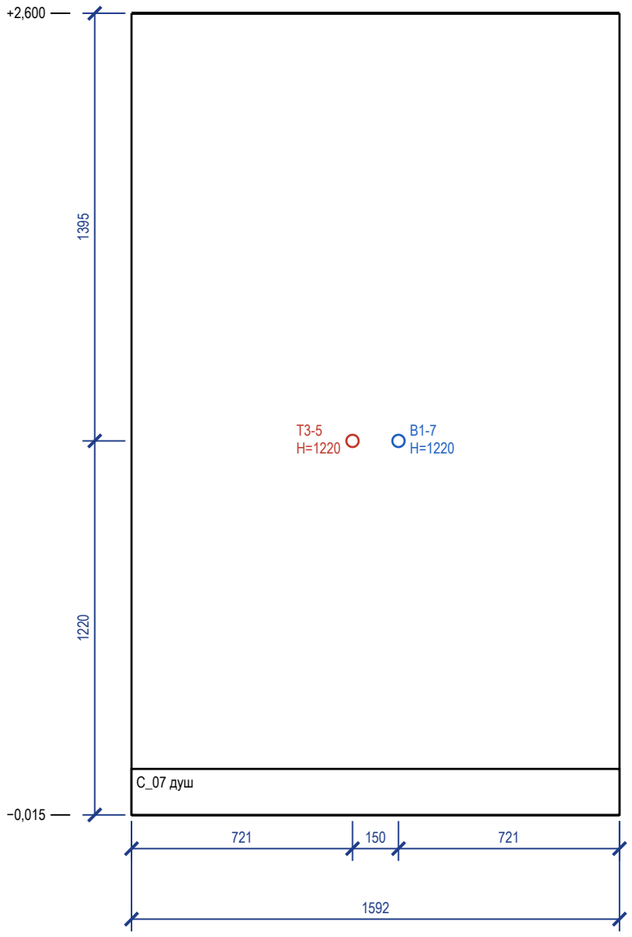


## Стена Г (М 1:20)

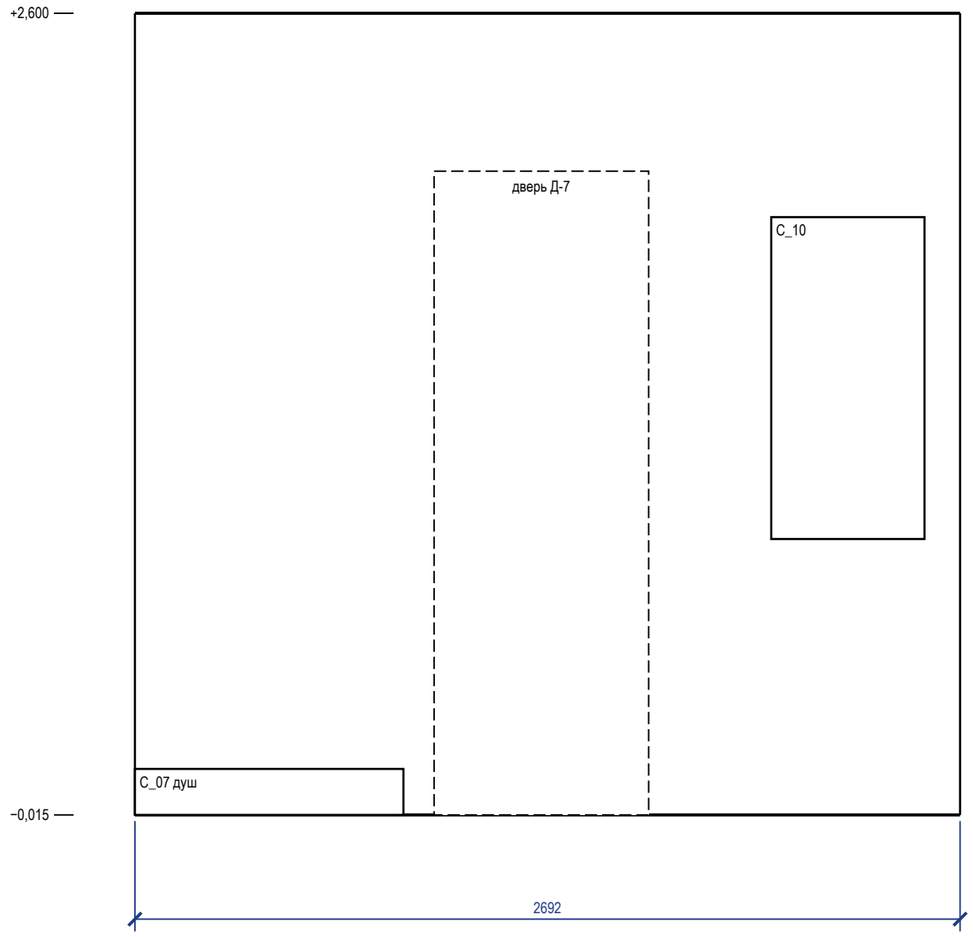


## Ведомость привязок выводов (от чистого пола и угла)

| Код | Прибор | Ø | H, мм | Привязка, мм |
|---|---|---|---|---|
| B1-7 | C_07 душ | ½" | 1220 | ст. В: 871 от лев. угла |
| T3-5 | C_07 душ | ½" | 1220 | ст. В: 721 от лев. угла |

## Условные обозначения

- вывод B1 (код — в ведомости привязок)
- вывод T3 (код — в ведомости привязок)
- вывод K1 (код — в ведомости привязок)
- сантехприбор по расстановке (габарит модели)
- дверной проём; окно — сплошной контур

## Примечания

1. Габариты и высоты приборов, межосевые смесителей и места кранов — по паспортам выбранных приборов, сверяются до разметки стен.
2. Высоты Н — от чистого пола помещения, мм; отметка чистого пола и потолка — у левого края вида (от ±0,000 объекта). Привязки — от левого чистового угла вида (облицовка стен вычтена), как на развёртках стен.
3. Выводы в полу (К1-1): трап, лоток, выпуск отдельностоящей ванны, подвод к стойке напольного смесителя — на развёртке их нет; место и пирог пола лист «Схема разводки» (профиль К1, узел 1).
4. Стояки в помещении: Ст К1-1 Ø110, Ст В1-1 Ø32, Ст Т3-1 Ø32 — положение на плане выводов; выводы подключаются к ним по схеме разводки.
5. Ревизионные люки (арматура и ревизии у С_07 300×400, стена В у С_07, предложение): привязка к углу — по раскладке плитки, подтверждается обмером.
6. Ревизионные люки к арматуре и ревизиям в данных не заданы: место и размер не определены (записи реестра нет).
7. Помещение «Санузел гостевой» — 2 листа: стены 1) А, Б; 2) В, Г.
8. Расчёт систем водоснабжения и канализации и подбор оборудования выполняет проектная организация; лист задаёт места и высоты выводов.

| | | | | |
|---|---|---|---|---|
| | Лист | № док. | Подпись | Дата |
| Дизайнер | Кырлан А.С. | | | 04.11.26 |

Проект: Квартира с кабинетом — **М 1:20**

Развёртки мокрых зон: выводы ВК. Санузел гостевой (лист 2 из 2)

| Стадия | Лист | Листов |
|---|---|---|
| П | 51 | 127 |


| Поз. | Наименование и техническая характеристика | Тип, марка, обозначение документа | Код продукции | Поставщик | Ед. изм. | Кол. | Масса 1 ед., кг | Примечание |
|---|---|---|---|---|---|---|---|---|
| | Санитарные приборы | | | | | | | |
| 1 | Ванна отдельностоящая из литого камня 1700×800 мм, выпуск в пол; донный клапан, перелив и сифон отдельной позицией | ванна отдельностоящая овальная 1700×800, литой камень; смеситель напольный | | выбор заказчика | шт | 1 | | C_01 |
| 2 | Унитаз подвесной безободковый, с сиденьем микролифт, крепёж и звукоизолирующая прокладка | Jacob Delafon Struktura EDF102-00 | | выбор заказчика | шт | 2 | | C_04, C_08 |
| 3 | Инсталляция для подвесного унитаза: рама высотой 1120 мм, бачок, клавиша смыва (ось клавиши 1050 мм от чистого пола) | аналог | | выбор заказчика | шт | 2 | | C_04 — короб ГКЛВ общий с C_05; C_08 короб ГКЛВ |
| 4 | Раковина накладная 600×450 мм, на столешницу тумбы, с переливом | раковина накладная овальная, две на тумбе 1500 | | выбор заказчика | шт | 2 | | C_02, C_03 |
| 5 | Умывальник из травертина 540×400 мм на консоли, с переливом | раковина 540 на консоли, травертин | | выбор заказчика | шт | 1 | | C_09 |
| 6 | Биде подвесное, крепёж и звукоизолирующая прокладка | биде подвесное | | выбор заказчика | шт | 1 | | C_05 |
| 7 | Инсталляция для подвесного биде: рама с крепёжными шпильками, водорозетками ½" (ХВ, ГВ) и выпуском Ø50 | аналог | | выбор заказчика | шт | 1 | | C_05; короб ГКЛВ общий с C_04 |
| 8 | Трап душевой с гидрозатвором и фланцем под гидроизоляцию, монтажная высота по паспорту | аналог | | выбор заказчика | шт | 1 | | C_07; узел 1 схема разводки |
| 9 | Мойка кухонная врезная / подстольная, с переливом, ориентир 700×480 мм — в модуле M_15 шириной 800 мм, вырез по шаблону модели | аналог | | с кухонной мебелью | шт | 1 | | M_15 |
| 10 | Полотенцесушитель электрический, IP44, с терморегулятором | аналог | | выбор заказчика | шт | 2 | | C_06, C_10 |
| | Смесители, сифоны и арматура приборов | | | | | | | |
| 11 | Смеситель для ванны напольный (стойка) однорычажный, с ручным душем; встраиваемая часть в пол — до стяжки | аналог | | выбор заказчика | шт | 1 | | C_01 |
| 12 | Смеситель для накладной раковины однорычажный, высокий излив, с донным клапаном | аналог | | выбор заказчика | шт | 2 | | C_02, C_03 |
| 13 | Смеситель для умывальника однорычажный, с донным клапаном | аналог | | выбор заказчика | шт | 1 | | C_09 |
| 14 | Душевая система скрытого монтажа с термостатом: встраиваемая часть, верхний душ, ручная лейка | аналог | | выбор заказчика | шт | 1 | | C_07; встраиваемая часть — до плитки |
| 15 | Смеситель кухонный однорычажный, высокий излив | аналог | | выбор заказчика | шт | 1 | | M_15 |
| 16 | Смеситель для биде однорычажный, с донным клапаном | аналог | | выбор заказчика | шт | 1 | | C_05 |
| 17 | Сифон для отдельностоящей ванны с донным клапаном и переливом, выпуск в пол Ø40/50 | аналог | | выбор заказчика | шт | 1 | | C_01 |
| 18 | Сифон для умывальника бутылочный Ø32/40–50, с гофрой к выпуску | аналог | | выбор заказчика | шт | 3 | | C_02, C_03, C_09 |
| 19 | Сифон для биде Ø32/40–50 | аналог | | выбор заказчика | шт | 1 | | C_05 |
| 20 | Сифон для мойки Ø40/50 | аналог | | выбор заказчика | шт | 1 | | M_15 |
| 21 | Сифон для посудомоечной машины с обратным клапаном, на выводе слива Ø40 | аналог | | выбор заказчика | шт | 1 | | M_16 |
| 22 | Сифон для стиральной машины встраиваемый в стену Ø50, с обратным клапаном | аналог | | выбор заказчика | шт | 1 | | ОБ_03 |
| 23 | Кран угловой ½"×½" с гибкой подводкой 40 см (умывальники, биде, мойка) | аналог | | выбор заказчика | шт | 10 | | по 2 на прибор |
| 24 | Кран шаровой угловой ½"×¾" для подключения стиральной и посудомоечной машины | аналог | | выбор заказчика | шт | 2 | | ОБ_03, M_16 |
| | Трубопроводы | | | | | | | |
| 25 | Труба полипропиленовая PP-R PN20 Ø20×3,4 (B1) | ГОСТ 32415-2013 | | выбор заказчика | м | 25 | 0,17 | 15,3 + 7,0 + 10 % |
| 26 | Труба PP-R, армированная стекловолокном, PN20 Ø20×2,8 (Т3) | ГОСТ 32415-2013 | | выбор заказчика | м | 19 | 0,15 | 13,6 + 3,7 + 10 % |
| 27 | Труба канализационная ПП Ø40 (К1) | ГОСТ 32414-2013 | | выбор заказчика | м | 1 | | 0,3 + 0,6 + 10 % |
| 28 | Труба канализационная ПП Ø50 (К1) | ГОСТ 32414-2013 | | выбор заказчика | м | 16 | | 11,5 + 2,8 + 10 % |
| 29 | Труба канализационная ПП Ø110 (К1) | ГОСТ 32414-2013 | | выбор заказчика | м | 2,5 | | 1,7 + 0,4 + 10 % |
| | Фасонные части и выводы | | | | | | | |
| 30 | Отвод канализационный ПП 45° Ø40 | ГОСТ 32414-2013 | | выбор заказчика | шт | 2 | | 2 шт. на поворот |
| 31 | Отвод канализационный ПП 45° Ø50 | ГОСТ 32414-2013 | | выбор заказчика | шт | 16 | | 2 шт. на поворот |
| 32 | Отвод канализационный ПП 45° Ø110 | ГОСТ 32414-2013 | | выбор заказчика | шт | 12 | | 2 шт. на поворот |
| 33 | Тройник канализационный ПП 45° (врезки ветвей) | ГОСТ 32414-2013 | | выбор заказчика | шт | 10 | | |
| 34 | Ревизия канализационная ПП (после поворота трассы) | ГОСТ 32414-2013 | | выбор заказчика | шт | 8 | | доступ сохранить |
| 35 | Фитинги PP-R Ø20: тройники, угольники 90° (ветви и повороты B1, Т3) | ГОСТ 32415-2013 | | выбор заказчика | шт | 44 | | |
| 36 | Водорозетка PP-R Ø20×½" настенная, с креплением | ГОСТ 32415-2013 | | выбор заказчика | шт | 16 | | коды — лист выводов |
| 37 | Вывод в пол PP-R Ø20 под встраиваемую часть напольного смесителя (переход на ½" по паспорту смесителя) | ГОСТ 32415-2013 | | выбор заказчика | шт | 2 | | C_01 |
| | Узлы ввода, люки, короба | | | | | | | |
| 38 | Кран шаровой латунный Ду15 PN16 (отключение ввода) | аналог | | выбор заказчика | шт | 6 | | Ст В1-1, Ст Т3-1, Ст В1-2, Ст Т3-2, Ст В1-3, Ст Т3-3 |
| 39 | Фильтр сетчатый косой Ду15 | аналог | | выбор заказчика | шт | 6 | | |
| 40 | Счётчик воды крыльчатый Ду15 (ХВ, ГВ), с поверкой | аналог | | выбор заказчика | шт | 6 | | пломба УК |
| 41 | Клапан обратный Ду15 | аналог | | выбор заказчика | шт | 6 | | |
| 42 | Люк ревизионный нажимной под плитку 300×400 мм | аналог | | выбор заказчика | шт | 3 | | к стоякам и арматуре |
| 43 | Звукоизоляция стояка К1 в коробе: рулонный звукоизоляционный материал ≥ 10 мм, обмотка стояка на высоту этажа | аналог | | выбор заказчика | м | 8,1 | | Ст К1-1, Ст К1-2, Ст К1-3 (кухня) |
| 44 | Короб К1 над полом: профиль ПН/ПС, ГКЛВ 12,5 мм под плитку | аналог | | выбор заказчика | м | 11,2 | | сечение — лист разводки |

## Примечания

1. Форма 1 ГОСТ 21.110-2013, ширины граф изменены по п. 4.1. «Аналог» — аналог по характеристикам: модели внести до черновых работ, привязки выводов сверить по паспортам.
2. Бытовая техника не входит (показана арматура подключения), мойка — в комплекте кухни (марка — модуля кухни, как у столяра). Длины труб — трасса листа разводки + подъёмы + 10 %.
3. Стояк К1 в коробе — звукоизоляция стояка в коробе без жёсткого контакта короба с трубой.
4. Расчёт систем водоснабжения и канализации, диаметры магистралей и подбор оборудования выполняет проектная организация.

| | | | | | |
|---|---|---|---|---|---|
| | | | | | Проект: Квартира с кабинетом |
| | Лист | № док. | Подпись | Дата | Спецификация сантехнического оборудования |
| Дизайнер | Кырлан А.С. | | | 04.11.26 | |

| Стадия | Лист | Листов |
|---|---|---|
| П | 52 | 127 |

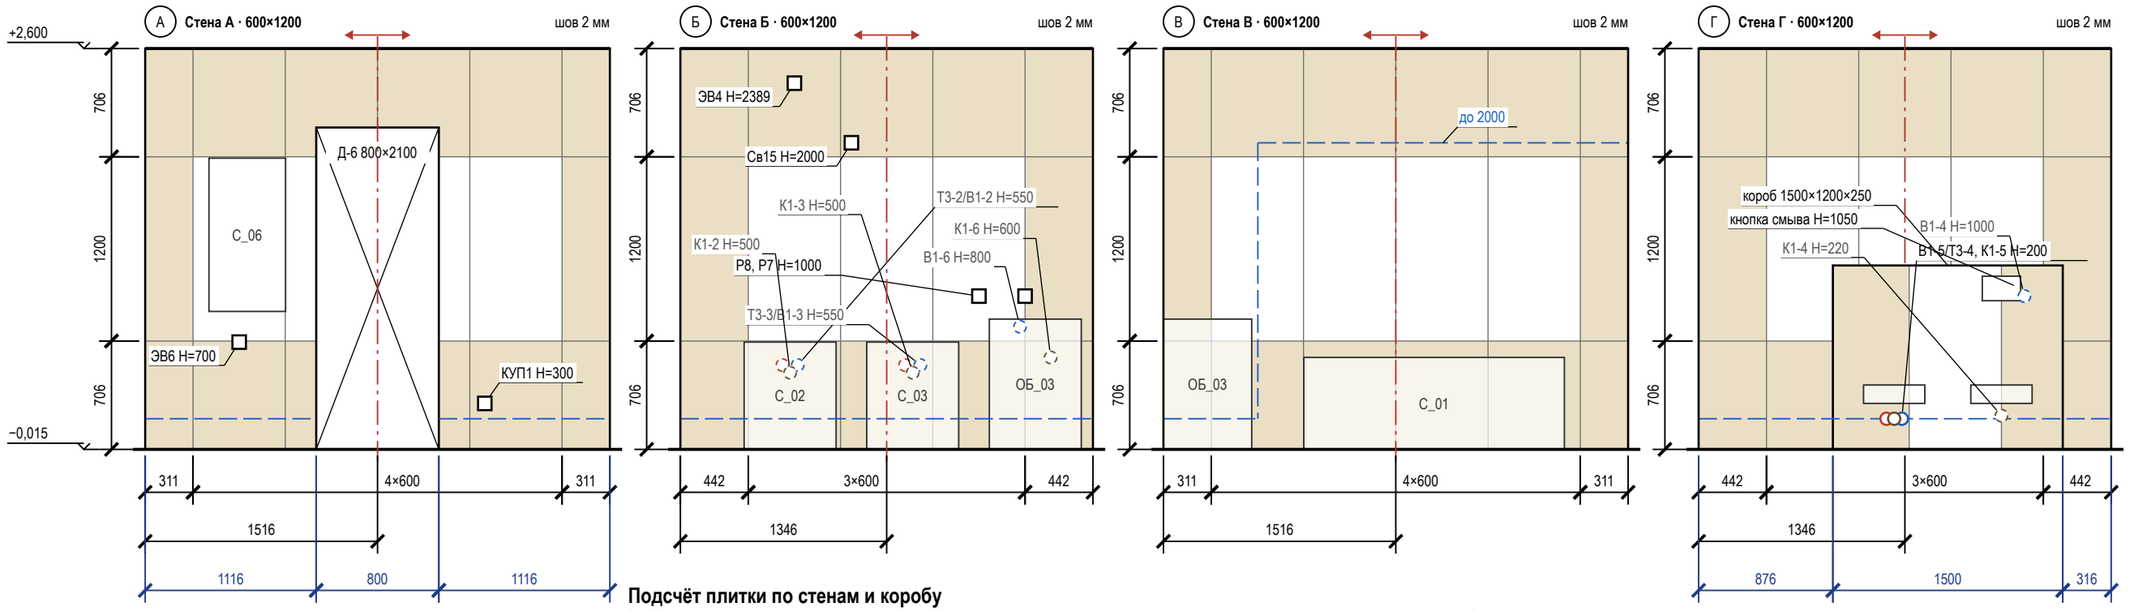


## Условные обозначения

- плитка целая; тонкая линия — шов
- плитка с подрезкой (размер — на цепочке)
- ось старта; стрелки — направление укладки
- верх гидроизоляции: 200 от ЧП, в мокрой зоне — «до …»
- проём — не облицовывается
- сантехприбор: габарит, высота по практике
- короб инсталляции, в нём кнопка смыва 250×160
- вывод В1 (код — в ведомости привязок)
- вывод Т3 (код — в ведомости привязок)
- вывод К1 (код — в ведомости привязок)
- вывод за прибором / в коробе (не на сетке)
- электроточка: марка и Н — по листам ЭОМ
- отметка уровня, м: ±0,000 — чистый пол жилых помещений
- низ потолка; серая полоса — стена без плитки
- А — обозначение стены А–Г (как на развёртках)

## Подсчёт плитки по стенам и коробу

| Поверхность | L × H, мм | S, м² | Целых | Подр. | С запасом | Подрезки: край / верх, мм |
|---|---|---|---|---|---|---|
| стена А | 3032 × 2615 | 6,37 | 2 | 16 | 20 | 311 / 311; 706 |
| стена Б | 2692 × 2615 | 7,17 | 3 | 12 | 17 | 442 / 442; 706 |
| стена В | 3032 × 2615 | 8,05 | 4 | 14 | 20 | 311 / 311; 706 |
| стена Г | 2692 × 2615 | 5,37 | 0 | 13 | 15 | 442 / 442; 706 |
| короб (ст. Г) | 1500×1200×250 | 2,77 | 1 | 7 | 9 | лицо 399 / 600 / 497; бок. 250 |
| **Итого** | | **29,73** | **10** | **62** | **81** | |


## Сдвиг точек под раскладку

| Точка (ВК, ЭОМ) | Стена | Проект: от угла / Н | Под раскладку: от угла / Н | Сдвиг, мм |
|---|---|---|---|---|
| КУП1 | А | 2216 / 300 | 2118 / 300 | −98 на шов |
| Св15 | Б | 1116 / 2000 | 1045 / 2000 | −71 на шов |

## Примечания

1. Вид изнутри, стены по часовой стрелке А → Г. Высоты — от чистого пола (−0,015), отметки — от ±0,000. Раскладка от чистовых размеров (штукатурка 10 + клей 5 + плитка 9 мм), подрезки чистые; старт от оси стены, ряды от середины (две подрезки).
2. Облицовка до потолка (+2,600).
3. Точки из таблицы сдвигов переносятся до черновой разводки (ЭОМ — по тем же числам).
4. Выводы ВК стоят по оси прибора и с прибором не двигаются — привязки по «Плану выводов сантехники» без сдвига; вне сетки (В1-5/Т3-4, К1-5) — отверстие в плитке коронкой по той же привязке, плитку не сдвигать.
5. За приборами и в коробе (Т3-2/В1-2, К1-2, Т3-3/В1-3, К1-3, В1-6, К1-6, В1-4, К1-4) — штриховым кольцом.
6. Гидроизоляция: 200 мм от ЧП по периметру; над ванной — до 2000 и 300 мм за борт (СП 29.13330.2011, п. 7.2 — на высоту замачивания); углы — лентой; акт скрытых работ, пролив.
7. Короб 1500×1200×250: лицо 399 / 600 / 497 мм от оси кнопки смыва, боковины, полка; углы — запил 45° или профиль; за коробом плитку не кладут.

| | | | | | |
|---|---|---|---|---|---|
| | | | | | Проект: Квартира с кабинетом — **М 1:40** |
| | Лист | № док. | Подпись | Дата | Раскладка плитки. Ванная. Развёртки стен |
| Дизайнер | Кырлан А.С. | | | 04.11.26 | Стадия: П · Лист: 53 · Листов: 127 |

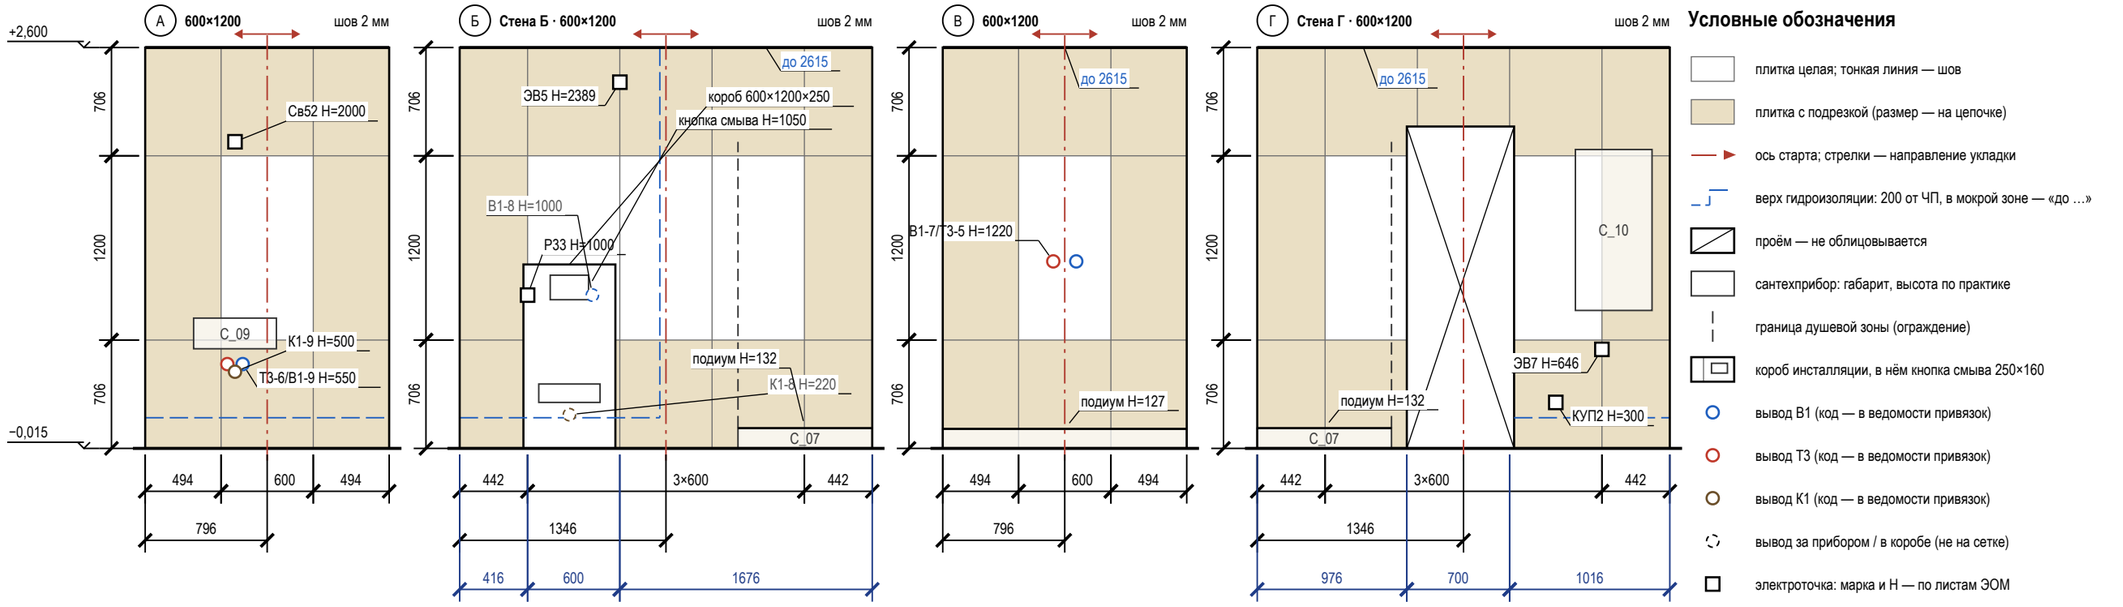


## Условные обозначения

- плитка целая; тонкая линия — шов
- плитка с подрезкой (размер — на цепочке)
- ось старта; стрелки — направление укладки
- верх гидроизоляции: 200 от ЧП, в мокрой зоне — «до …»
- проём — не облицовывается
- сантехприбор: габарит, высота по практике
- граница душевой зоны (ограждение)
- короб инсталляции, в нём кнопка смыва 250×160
- вывод В1 (код — в ведомости привязок)
- вывод Т3 (код — в ведомости привязок)
- вывод К1 (код — в ведомости привязок)
- вывод за прибором / в коробе (не на сетке)
- электроточка: марка и Н — по листам ЭОМ
- отметка уровня, м: ±0,000 — чистый пол жилых помещений
- низ потолка; серая полоса — стена без плитки
- (А) обозначение стены А–Г (как на развёртках)

## Подсчёт плитки по стенам и коробу

| Поверхность | L × H, мм | S, м² | Целых | Подр. | С запасом | Подрезки: край / верх, мм |
|---|---|---|---|---|---|---|
| стена А | 1592 × 2615 | 4,29 | 1 | 8 | 10 | 494 / 494; 706 |
| стена Б | 2692 × 2615 | 6,45 | 2 | 13 | 17 | 442 / 442; 706 |
| короб (ст. Б) | 600×1200×250 | 1,47 | 1 | 3 | 5 | лицо 600; бок. 250 |
| стена В | 1592 × 2615 | 4,29 | 1 | 8 | 10 | 494 / 494; 706 |
| стена Г | 2692 × 2615 | 5,70 | 0 | 13 | 15 | 442 / 442; 706 |
| **Итого** | | **22,19** | **5** | **45** | **57** | |


## Сдвиг точек под раскладку

| Точка (ВК, ЭОМ) | Стена | Проект: от угла / Н | Под раскладку: от угла / Н | Сдвиг, мм |
|---|---|---|---|---|
| Св52 | А | 586 / 2000 | 495 / 2000 | −91 на шов |

## Примечания

1. Вид изнутри, стены по часовой стрелке А → Г. Высоты — от чистого пола (−0,015), отметки — от ±0,000. Раскладка от чистовых размеров (штукатурка 10 + клей 5 + плитка 9 мм), подрезки чистые; старт — от оси стены, ряды от середины (две подрезки).
2. Облицовка до потолка (+2,600).
3. Точки из таблицы сдвигов переносятся до черновой разводки (ЭОМ — по тем же числам).
4. Выводы ВК стоят по оси прибора и с прибором не двигаются — привязки по «Плану выводов сантехники» без сдвига; вне сетки (Т3-6/В1-9, К1-9) — отверстие в плитке коронкой по той же привязке, плитку не сдвигать.
5. За приборами и в коробе (В1-8, К1-8) — штриховым кольцом.
6. Подиум душа C_07: верх у решётки трапа +0,105 (h 120 мм), к стенам поднимается уклоном к трапу — «подиум Н=…» на развёртке — верх подиума у этой стены; облицовка стен в зоне душа — от верха подиума, грань ступени — плиткой пола. Выводы В1-7, Т3-5: Н=1220 от чистого пола помещения = 1100 от верха подиума у трапа.
7. Гидроизоляция: 200 мм от ЧП по периметру; у душа — на всю высоту стен душевой зоны и 500 мм за край душевой зоны (СП 29.13330.2011, п. 7.2 — на высоту замачивания); углы — лентой; акт скрытых работ, пролив.
8. Короб 600×1200×250: лицо 600 мм от оси кнопки смыва, боковины, полка; углы — запил 45° или профиль; за коробом плитку не кладут.

| | | | | | | |
|---|---|---|---|---|---|---|
| | | | | | Проект: Квартира с кабинетом | **М 1:40** |
| | Лист | № док. | Подпись | Дата | | |
| Дизайнер | Кырлан А.С. | | | 04.11.26 | Раскладка плитки. Санузел гостевой. Развёртки стен | Стадия: П; Лист: 54; Листов: 127 |

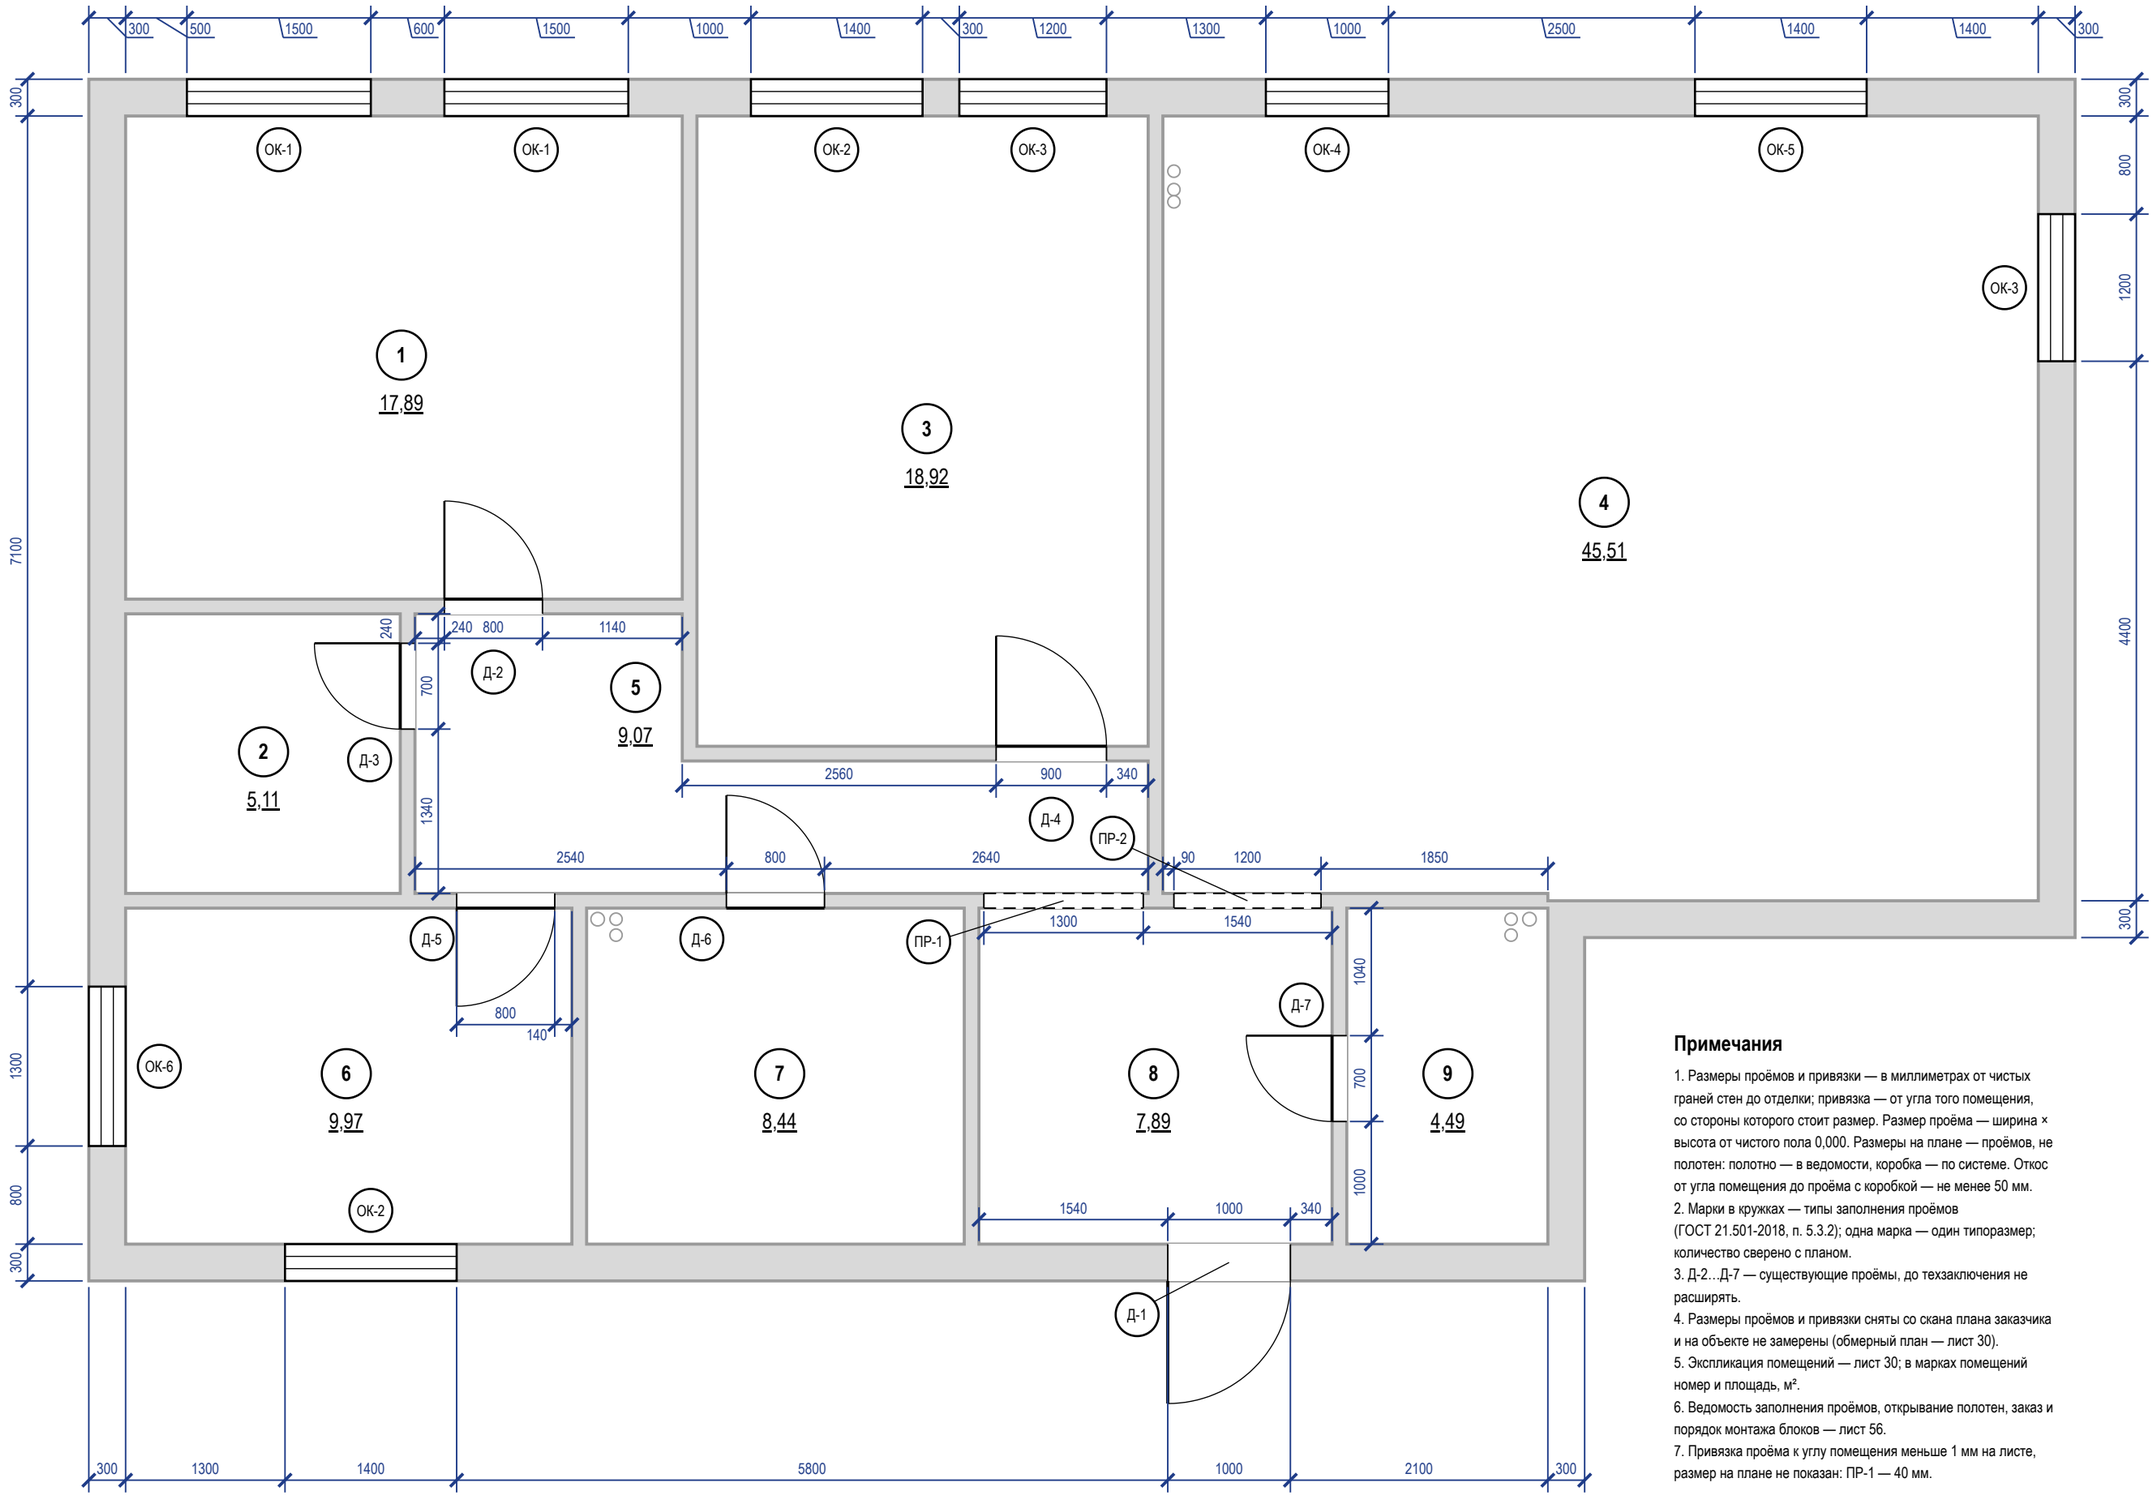


## Примечания


1. Размеры проёмов и привязки — в миллиметрах от чистых граней стен до отделки; привязка — от угла того помещения, со стороны которого стоит размер. Размер проёма — ширина × высота от чистого пола 0,000. Размеры на плане — проёмов, не полотен: полотно — в ведомости, коробка — по системе. Откос от угла помещения до проёма с коробкой — не менее 50 мм.
2. Марки в кружках — типы заполнения проёмов (ГОСТ 21.501-2018, п. 5.3.2); одна марка — один типоразмер; количество сверено с планом.
3. Д-2…Д-7 — существующие проёмы, до техзаключения не расширять.
4. Размеры проёмов и привязки сняты со скана плана заказчика и на объекте не замерены (обмерный план — лист 30).
5. Экспликация помещений — лист 30; в марках помещений номер и площадь, м².
6. Ведомость заполнения проёмов, открывание полотен, заказ и порядок монтажа блоков — лист 56.
7. Привязка проёма к углу помещения меньше 1 мм на листе, размер на плане не показан: ПР-1 — 40 мм.

| | | | | | | |
|---|---|---|---|---|---|---|
| | | | | | Проект: Квартира с кабинетом | **М 1:50** |
| | Лист | № док. | Подпись | Дата | | |
| Дизайнер | Кырлан А.С. | | | 04.11.26 | План размещения дверей | Стадия: П; Лист: 55; Листов: 127 |

## Ведомость заполнения проёмов

| Марка | Наименование, обозначение | Проём ш×в, мм | Полотно (расч.) | Кол. | Откр. | Отделка полотна | Фурнитура | Прим. |
|---|---|---|---|---|---|---|---|---|
| Д-1 | Блок дверной входной, ГОСТ 31173-2016 | 1000×2100 | блок задать | 1 | Л | в комплекте блока | в комплекте блока (замки, глазок) | наружу |
| Д-2 | Дверь скрытого монтажа, UNION FILO-60 Piatto | 800×2100 | 700×2000 | 1 | П | окраска No. 15 с двух сторон | скрытые петли 3D, магнитный замок | |
| Д-3 | Дверь скрытого монтажа, UNION FILO-60 Piatto | 700×2100 | 600×2000 | 1 | Л | V503 — пом. 2, No. 15 — пом. 5 | скрытые петли 3D, магнитный замок | |
| Д-4 | Дверь скрытого монтажа, UNION FILO-60 Piatto | 900×2100 | 800×2000 | 1 | П | окраска No. 15 с двух сторон | скрытые петли 3D, магнитный замок | |
| Д-5 | Дверь скрытого монтажа, UNION FILO-60 Piatto | 800×2100 | 700×2000 | 1 | Л | окраска No. 15 с двух сторон | скрытые петли 3D, магнитный замок | |
| Д-6 | Дверь скрытого монтажа, UNION FILO-60 Piatto | 800×2100 | 700×2000 | 1 | П | в тон облицовки с двух сторон | скрытые петли 3D, магнитный замок, фиксатор WC | пом. 7; порог 15 |
| Д-7 | Дверь скрытого монтажа, UNION FILO-60 Piatto | 700×2100 | 600×2000 | 1 | Л | No. 15 — пом. 8, в тон облицовки — пом. 9 | скрытые петли 3D, магнитный замок, фиксатор WC | порог 15 |
| ПР-1 | Портал без заполнения | 1300×2100 | | 1 | | | | б/п |
| ПР-2 | Портал без заполнения | 1200×2100 | | 1 | | | | б/п |
| ОК-1 | Блок оконный, ГОСТ 23166-2021 | 1500×1600 | | 2 | | | | низ 800 |
| ОК-2 | Блок оконный, ГОСТ 23166-2021 | 1400×1600 | | 2 | | | | низ 800 |
| ОК-3 | Блок оконный, ГОСТ 23166-2021 | 1200×1600 | | 2 | | | | низ 800 |
| ОК-4 | Блок оконный, ГОСТ 23166-2021 | 1000×1400 | | 1 | | | | низ 1000 |
| ОК-5 | Блок оконный, ГОСТ 23166-2021 | 1400×1600 | | 1 | | | | низ 900 |
| ОК-6 | Блок оконный, ГОСТ 23166-2021 | 1300×1600 | | 1 | | | | низ 800 |

**Схемы дверных блоков (1:50) — вид со стороны открывания; вершина треугольника — сторона петель**

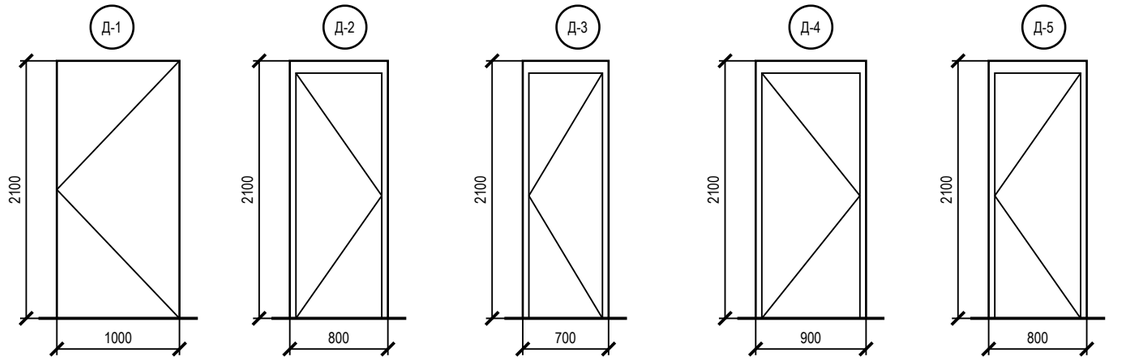



блок — по ГОСТ 31173 откр. Л

полотно 700×2000 (расч.) откр. П

полотно 600×2000 (расч.) откр. Л

полотно 800×2000 (расч.) откр. П

полотно 700×2000 (расч.) откр. Л

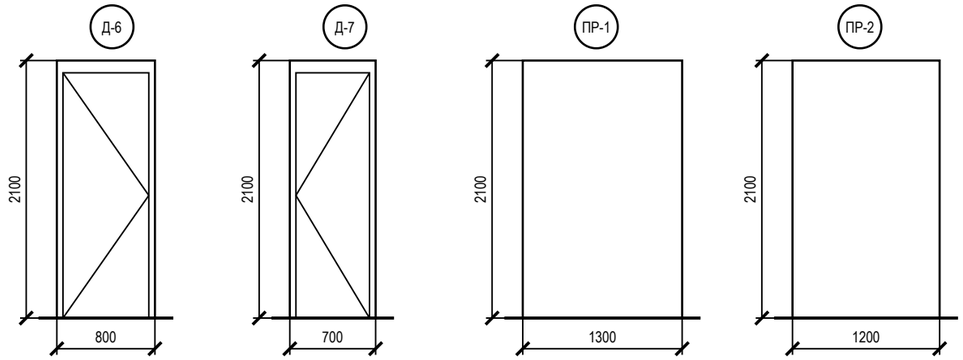


полотно 700×2000 (расч.) откр. П

полотно 600×2000 (расч.) откр. Л

без заполнения


без заполнения

## Примечания

1. Марки проёмов — те же, что на плане размещения дверей (лист 55); привязки проёмов — там же.
2. Открывание: Л — петли слева, П — справа, если смотреть со стороны, куда открывается полотно (на себя).
3. Скрытые двери (Д-2…Д-7): проём замерить в чистоте; блок заказать до штукатурки (≈ 30 дн.), короб ставить до штукатурки; полотно навесить после чистовой отделки, красить в цвет стен. Порядок — практика монтажа, изготовитель подтверждает.
4. Полотно «расч.» — по проёму и ряду изделия с запасом по каталогам, заказ — по таблице проёмов модели; Д-2…Д-7: проём 2100, а под полотно 2000 по каталогам нужен 2050–2080, под 2100 — 2150–2180: высоту проёма — по модели; Д-1: входной блок по ГОСТ 31173-2016 — задать при выборе блока.

| | | | | | |
|---|---|---|---|---|---|
| | | | | | Проект: Квартира с кабинетом |
| | Лист | № док. | Подпись | Дата | |
| Дизайнер | Кырлан А.С. | | | 04.11.26 | Ведомость заполнения проёмов |

| Стадия | Лист | Листов |
|---|---|---|
| П | 56 | 127 |

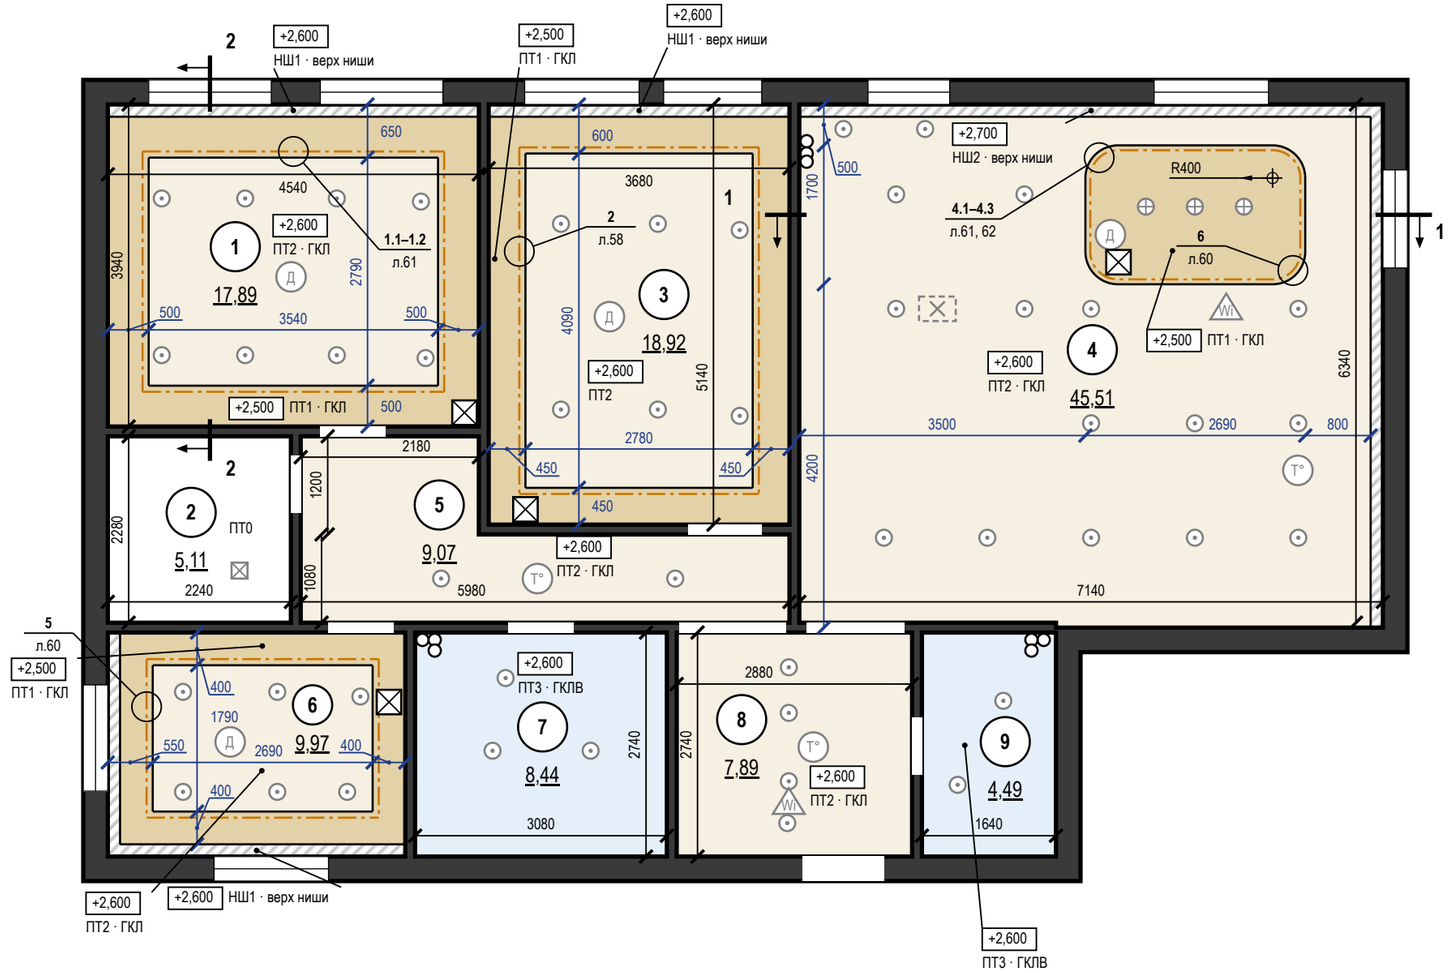


## Ведомость потолков

| Пом. | Марка | Конструкция | Низ / верх ниши | S, м² | Q |
|---|---|---|---|---|---|
| 1 | ПТ1 | ГКЛ П113, короб LED | +2,500 | 7,33 | Q3 |
| 1 | ПТ2 | ГКЛ П113 | +2,600 | 9,88 | Q3 |
| 1 | НШ1 | ниша под шторы 150×100 | +2,600 | 0,68 | |
| 2 | ПТ0 | Существующий потолок, окраска | +2,700 | 5,11 | |
| 3 | ПТ1 | ГКЛ П113, короб LED | +2,500 | 7,00 | Q3 |
| 3 | ПТ2 | ГКЛ П113 | +2,600 | 11,37 | Q3 |
| 3 | НШ1 | ниша под шторы 150×100 | +2,600 | 0,55 | |
| 4 | ПТ1 | ГКЛ П113, остров + LED | +2,500 | 4,43 | Q3 |
| 4 | ПТ2 | ГКЛ П113 | +2,600 | 39,07 | Q3 |
| 4 | НШ2 | ниша под шторы 150×100 | +2,700 | 2,01 | |
| 5 | ПТ2 | ГКЛ П113 | +2,600 | 9,07 | Q3 |
| 6 | ПТ1 | ГКЛ П113, короб LED | +2,500 | 4,22 | Q3 |
| 6 | ПТ2 | ГКЛ П113 | +2,600 | 4,81 | Q3 |
| 6 | НШ1 | ниша под шторы 150×100 | +2,600 | 0,94 | |
| 7 | ПТ3 | ГКЛВ П113 | +2,600 | 8,44 | Q3 |
| 8 | ПТ2 | ГКЛ П113 | +2,600 | 7,89 | Q3 |
| 9 | ПТ3 | ГКЛВ П113 | +2,600 | 4,49 | Q3 |
| | | **Итого** | | **127,29** | |

## Ведомость вырезов и закладных в потолке

| Марка | Устройство | Кол. | Пом. |
|---|---|---|---|
| | Светильник встраиваемый (марки — план освещения) | 47 | 1, 3, 4, 5, 6, 7, 8, 9 |
| | Светильник накладной (марки — план освещения) | 1 | 2 |
| | Светильник подвесной (марки — план освещения) | 3 | 4 |
| ИП1, ИП2, ИП4, ИП7 | Извещатель дымовой | 4 | 1, 3, 4, 6 |
| ИП5, ИП6, ИП3 | Извещатель тепловой | 3 | 4, 5, 8 |
| AP2, AP1 | Точка доступа Wi-Fi, PoE | 2 | 4, 8 |
| M_19 | Вытяжка островная: закладная под подвес к плите, проход штанги и вывод питания через ГКЛ — по паспорту модели | 1 | 4 |
| | Люк ревизии 300×300 | 4 | 1, 3, 4, 6 |


## Примечания

1. За отметку ±0,000 принят уровень чистого пола сухих помещений (готовое покрытие), а не существующего пола; пол пом. 7, 9 — −0,015; верх плиты перекрытия −0,064 — расчётный по пирогу пола, не замерен; существующий пол снимается до плиты, его отметка не замерена. Отметки в прямоугольниках — низ потолка; низ перекрытия +2,700. Марка потолка — одна конструкция и отметка на весь альбом.
2. Размеры помещений в свету (ширина × длина, мм), не поместившиеся на плане: пом. 4 — 7140 × 6340, 4000 × 60; пом. 6 — 3640 × 2740; пом. 9 — 1640 × 2740.
3. Потолки ГКЛ — каркасная система П113: подвесы через 1000 (с запасом: СП 163, табл. 14 — до 1100 при 0,15 кН/м²), несущие профили через 500, основные через 1200 мм; листы — поперёк несущих профилей. В помещениях 7, 9 — ГКЛВ на оцинкованном каркасе.
4. Нижний уровень — пояс-короб по периметру шириной 500, 450, 400 мм, верхний — поле внутри пояса: пом. 1, 3, 6.
5. LED-лента в алюминиевом профиле посередине карниза короба шириной 500, 450, 400 мм (узел 1 — пом. 1, лист 58; узел 2 — пом. 3, лист 58; узел 5 — пом. 6, лист 60); длина по плану: пом. 1 — 13,3 м (в плане освещения 13,3); пом. 3 — 14,3 м (в плане освещения 14,3); пом. 6 — 9,6 м (в плане освещения 9,6).
6. Ниши под шторы 150×100 мм — на всю длину стены с окном; карниз — на закладной до обшивки (узел 4 — пом. 1, 3, 6, лист 59; узел 3 — пом. 4, лист 58).
7. Светильники и потолочные устройства — подложка с планов освещения, слаботочных систем и вентиляции (положение — по ним); вырезы и закладные — по ведомости на листе, до обшивки; отверстия не совмещать с профилями, глубина корпуса светильника до 70 мм.
8. Разрезы 1–1, 2–2 — на листе 58; высоты мебели и дверных блоков сверены с низом потолка в разрезах; гибка бортов фигур и ленты ниш — там же; размеры фигурных уровней — фрагмент 1 (лист 59).
9. Шпаклевание ГКЛ и условия приёмки — Q3: рассеянный дневной свет, осмотр с 2 м; боковой свет не оценивается.
10. Люки ревизии 300×300 мм — по центру блоков питания LED (БП1, БП2, БП4, БП6; координаты — план освещения).
11. ПТ0 — пом. 2: существующий потолок, окраска, без подвесного потолка, низ +2,700; материал и цвет — по ведомости отделки.
12. Сечения потолков М 1:10: пом. 3 — 3.1, 3.2 (лист 61); пом. 6 — 6.1, 6.2 (лист 62).

| | | | | | |
|---|---|---|---|---|---|
| | | | | | Проект: Квартира с кабинетом — **М 1:75** |
| | Лист | № док. | Подпись | Дата | |
| Дизайнер | Кырлан А.С. | | | 04.11.26 | План потолков — Стадия: П; Лист: 57; Листов: 127 |


## Разрез 1–1 (М 1:40)

Пом. 4 Кухня-гостиная; линия разреза — план потолков, лист 57

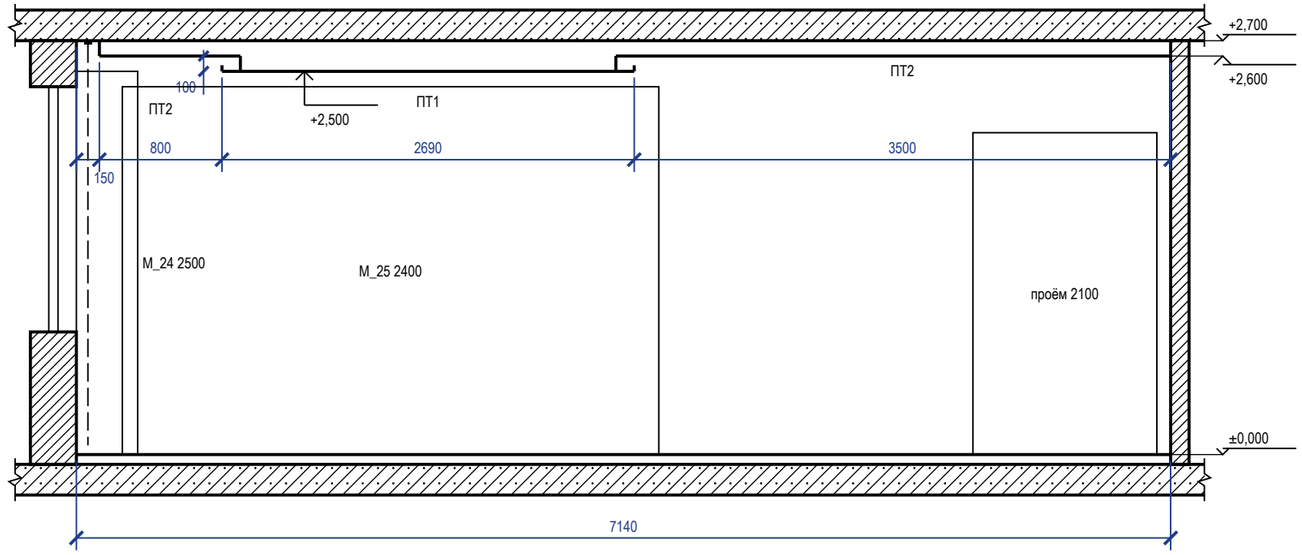


## Разрез 2–2 (М 1:40)

Пом. 1 Спальня; линия разреза — план потолков, лист 57

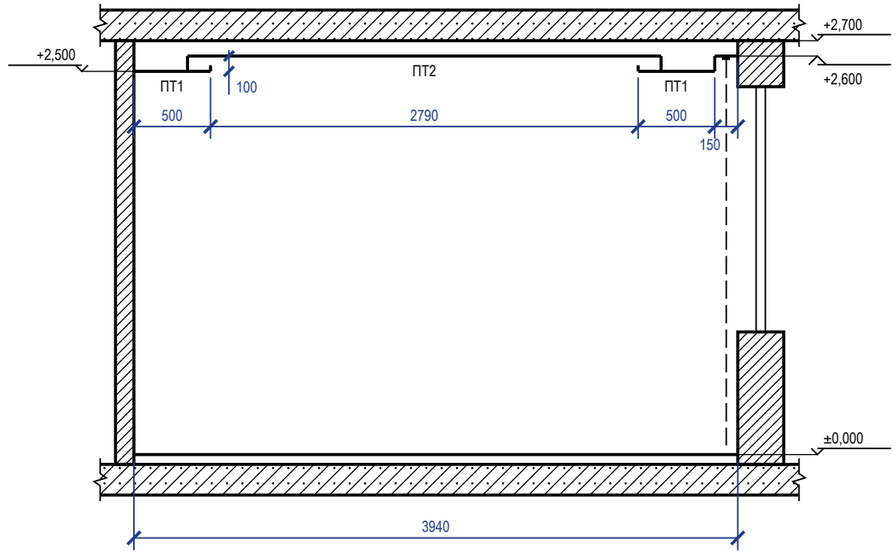


## 1 Короб с LED-подсветкой (М 1:10)

Пом. 1; карниз 150×100, щель под свет 60 мм




1 — плита перекрытия
2 — подвес прямой, шаг 1000 мм
3 — ПП 60×27: несущие через 500, основные через 1200 мм
4 — ГКЛ 12,5 по П113 — верхний уровень
5 — задняя стенка и бортик карниза — ГКЛ 12,5
6 — ПН 28×27 по периметру, к стене через 500 мм
7 — LED-лента в алюминиевом профиле
8 — низ короба — ГКЛ 12,5 по ПП 60×27

## 2 Короб с LED-подсветкой (М 1:10)

Пом. 3; карниз 150×100, щель под свет 60 мм





1 — плита перекрытия
2 — подвес прямой, шаг 1000 мм
3 — ПП 60×27: несущие через 500, основные через 1200 мм
4 — ГКЛ 12,5 по П113 — верхний уровень
5 — задняя стенка и бортик карниза — ГКЛ 12,5
6 — ПН 28×27 по периметру, к стене через 500 мм
7 — LED-лента в алюминиевом профиле
8 — низ короба — ГКЛ 12,5 по ПП 60×27

## Условные обозначения

- плита перекрытия в сечении
- стена в сечении
- потолок ГКЛ в сечении; под линией — марка потолка (план потолков)
- мебель и дверные проёмы за секущей плоскостью; число — марка и верх от чистого пола, мм
- портьера в нише под шторы

## 3 Ниша под шторы (М 1:10)

Пом. 4; без подсветки; закладные под карниз — до обшивки

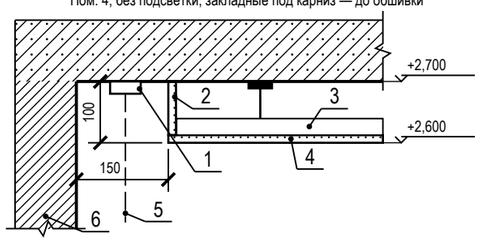


1 — карниз (шина), высота с верхом портьеры 80 мм
2 — стенка ниши — ГКЛ 12,5
3 — ПП 60×27 — каркас короба
4 — низ короба нижнего уровня — ГКЛ 12,5
5 — портьера
6 — стена с окном


## Примечания

1. Разрезы — по линиям 1–1, 2–2 на плане потолков (лист 57). Отметки — от ±0,000 чистого пола, м; размеры — мм.
2. Высоты мебели и дверных блоков за секущей плоскостью сверены с низом потолка над ними: верх ниже низа короба и поля.
3. ГКЛ 12,5 мм по каркасу П113; перепад уровней и бортик карниза — ГКЛ по ПП 60×27 (узел 1 — на этом листе; узел 2 — на этом листе; узел 5 — лист 60). Ниша под шторы — на всю длину стены с окном, карниз на закладной до обшивки (узел 4 — лист 59; узел 3 — на этом листе).
4. Толщины плит перекрытия и пирога пола показаны условно.
5. Сечения потолков по помещениям М 1:10 (отметки помещения, профили, подвесы, крепёж, изделия) — листы 61–62.
6. Ведомость объёмов потолков (лист ГКЛ, профиль, подвесы, лента, блоки питания, люки) — на листе 59.
7. Фрагмент 1 — помещение с фигурными уровнями (размеры фигур, радиусы, отметки) — на листе 59.

| | | | | | | |
|---|---|---|---|---|---|---|
| | | | | | Проект: Квартира с кабинетом | М 1:40; 1:10 |
| | Лист | № док. | Подпись | Дата | Разрезы и узлы потолков | Стадия / Лист / Листов |
| Дизайнер | Кырлан А.С. | | | 04.11.26 | | П / 58 / 127 |

## Фрагмент 1. Пом. 4 Кухня-гостиная — уровни потолка (М 1:50)

Цепочки — от чистых граней стен; отметки — низ уровня от ±0,000

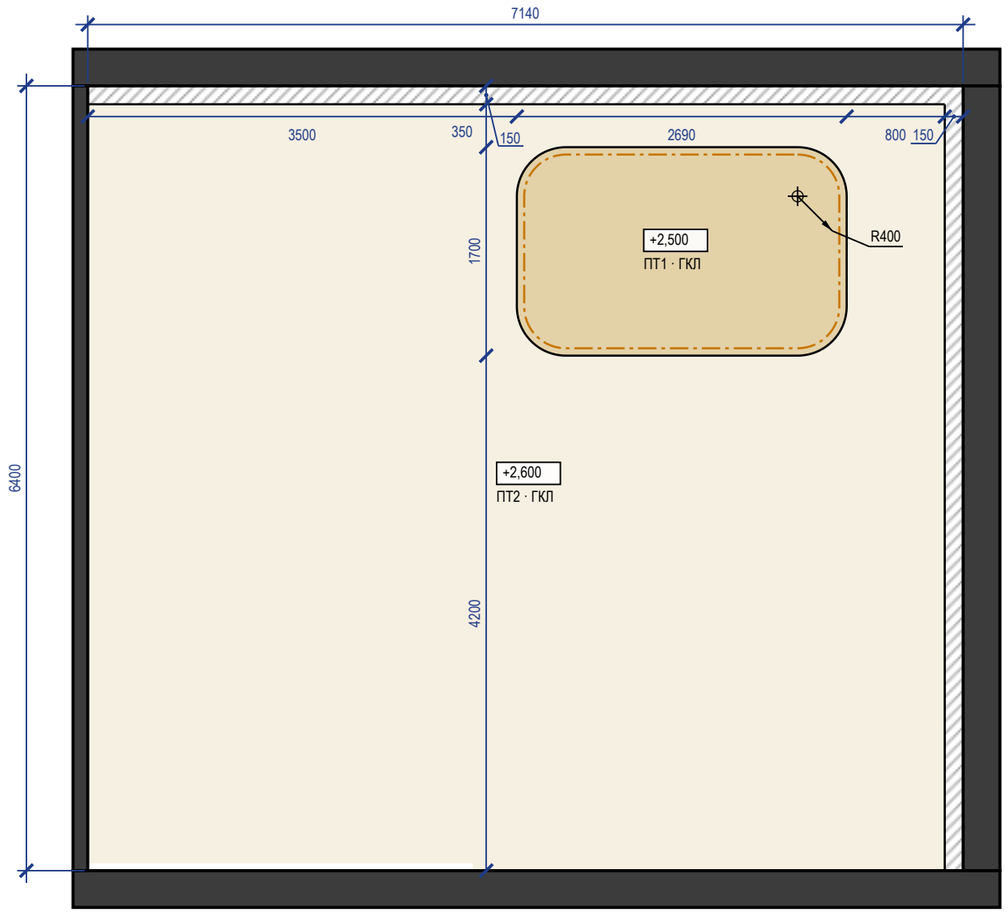



ПТ1 — низ +2,500 · ПТ2 — низ +2,600 · LED-лента в нише подсветки (карниз короба, ниша фигуры) · ниша под шторы

## Ведомость объёмов потолков

| Позиция | Ед. | Кол. | Пом. |
|---|---|---|---|
| Лист ГКЛ 12,5 | м² | 124,34 | 1, 3, 4, 5, 6, 8 |
| Лист ГКЛВ 12,5 | м² | 12,93 | 7, 9 |
| Лист ГКЛ арочный 6,5 | м² | 0,70 | 4 |
| Борта и карнизы (входят в площади листов выше) | м² | 15,46 | 1, 3, 4, 6 |
| Профиль ПП 60×27 | м | 364,38 | 1, 3, 4, 5, 6, 7, 8, 9 |
| Профиль ПН 28×27 | м | 309,84 | 1, 3, 4, 5, 6, 7, 8, 9 |
| Подвес прямой | шт. | 141 | 1, 3, 4, 5, 6, 7, 8, 9 |
| Анкер-клин к плите | шт. | 141 | 1, 3, 4, 5, 6, 7, 8, 9 |
| Шуруп TN 3,5×25 | шт. | 3165 | 1, 3, 4, 5, 6, 7, 8, 9 |
| Лента армирующая для швов | м | 165,14 | 1, 3, 4, 5, 6, 7, 8, 9 |
| Шпаклёвка для швов | кг | 55,05 | 1, 3, 4, 5, 6, 7, 8, 9 |
| Грунтовка (швы) | л | 13,76 | 1, 3, 4, 5, 6, 7, 8, 9 |
| Лента разделительная по периметру | м | 122,60 | 1, 3, 4, 5, 6, 7, 8, 9 |
| Сплошная шпаклёвка и окраска (площадь развёртки) | м² | 137,62 | 1, 3, 4, 5, 6, 7, 8, 9 |
| Лента LED | м | 44,88 | 1, 3, 4, 6 |
| Требуемая мощность блоков питания | Вт | 560 | 1, 3, 4, 6 |
| Установленная мощность блоков питания | Вт | 900 | 1, 3, 4, 6 |
| Блок питания LED | шт. | 4 | 1, 3, 4, 6 |
| Люк ревизии | шт. | 4 | 1, 3, 4, 6 |

## 4 Ниша под шторы (М 1:10)

Пом. 1, 3, 6; без подсветки; закладные под карниз — до обшивки

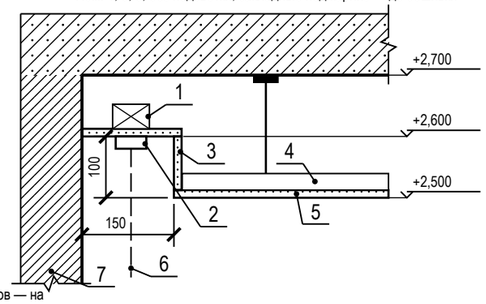


1 — закладная под карниз — брус 40×50
2 — карниз (шина), высота с верхом портьеры 80 мм
3 — стенка и потолок ниши — ГКЛ 12,5
4 — ПП 60×27 — каркас короба
5 — низ короба нижнего уровня — ГКЛ 12,5
6 — портьера
7 — стена с окном

## Примечания

1. ГКЛ 12,5 мм по каркасу П113; узлы коробов и ниш под шторы: узел 1 — лист 58; узел 2 — лист 58; узел 5 — лист 60; узел 4 — на этом листе; узел 3 — лист 58; условные обозначения разрезов — на листе 58.
2. Фрагмент 1 (план потолков — лист 57) — фигурные уровни потолка крупно: привязки краёв и центров фигур к чистым граням стен, радиусы (R) с центрами, хорда и стрелка дуги, отметки низа каждого уровня; цвета уровней — как на плане потолков.
3. Фигурные уровни: борт — ГКЛ по ПН с надрезами (на дуге шаг стоек борта 300 мм при R до 2500, 400 — до 5000) или по гнутому заводскому профилю (СП 163, 6.3.3); гибка: остров пом. 4 R400 — ГКЛ 6,5 мокрой гибкой (СП 163, табл. 9). Лента в нише фигуры по оси: остров пом. 4 — 7,7 м; узел ниши LED фигуры: узел 6 — лист 60 — пом. 4.
4. Ведомость объёмов — по геометрии плана потолков: Лист ГКЛ 12,5 — плоскости уровней + борта (без арочных участков); Лист ГКЛВ 12,5 — плоскости уровней + борта; Лист ГКЛ арочный 6,5 — кривая борта × высота борта и стенки ниши × 2 слоя (R400 мокрая гибка); Борта и карнизы — длина перепада × перепад; Профиль ПП 60×27 — S × (1/шаг несущ. + 1/шаг осн.) + стойки бортов; Профиль ПН 28×27 — периметр стен + 2 × перепады + карнизы; Подвес прямой — по раскладке: S уровня / (шаг осн. × шаг подвесов), пояс уже шага — ряд вдоль пояса, фигура — по контуру; шаг подвесов — не больше табл. 14 СП 163; Анкер-клин к плите — по одному на подвес (Knauf П113); Шуруп TN 3,5×25 — 23 шт./м² (Knauf П113, табл. 2 альбома П 11); Лента армирующая для швов — 1,2 м/м² листа (Knauf); Шпаклёвка для швов — 0,4 кг/м² листа, только швы (Knauf); Грунтовка (швы) — 0,1 л/м² листа, только швы (Knauf); Лента разделительная по периметру — периметр стен под потолком ГКЛ; Сплошная шпаклёвка и окраска (площадь развёртки) — плоскости + борта; расход — по паспорту материала (норма расхода на сплошной слой не подтверждена); Лента LED — по оси карниза и ниши фигуры (план потолков); Требуемая мощность блоков питания — Вт/м × длина × 1,3; Установленная мощность блоков питания — сумма мощностей блоков по плану освещения; Блок питания LED блоки потолочных лент по плану освещения (БП1, БП2, БП4, БП6); Люк ревизии — план потолков; без запаса на подрезку (при закупке листа: ×1,075 при S > 20 м², ×1,175 — 10–20 м², ×1,275 — < 10 м²).

| | | | | |
|---|---|---|---|---|
| | Лист | № док. | Подпись | Дата |
| Дизайнер | Кырлан А.С. | | | 04.11.26 |


Проект: Квартира с кабинетом — **М 1:50; 1:10**

Разрезы и узлы потолков (продолжение)

| Стадия | Лист | Листов |
|---|---|---|
| П | 59 | 127 |

## 5 Короб с LED-подсветкой (М 1:10)


Пом. 6; карниз 150×100, щель под свет 60 мм

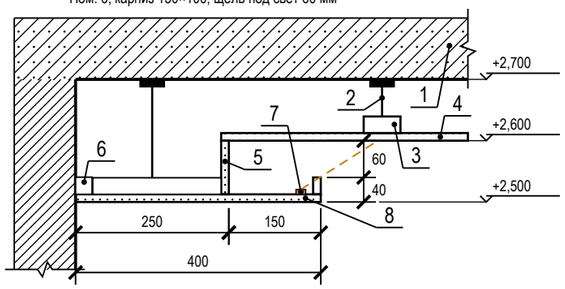


1 — плита перекрытия
2 — подвес прямой, шаг 1000 мм
3 — ПП 60×27: несущие через 500, основные через 1200 мм
4 — ГКЛ 12,5 по П113 — верхний уровень
5 — задняя стенка и бортик карниза — ГКЛ 12,5
6 — ПН 28×27 по периметру, к стене через 500 мм
7 — LED-лента в алюминиевом профиле
8 — низ короба — ГКЛ 12,5 по ПП 60×27

## 6 Ниша LED фигурного уровня (М 1:10)

Пом. 4; карниз 120×100, щель под свет 60 мм

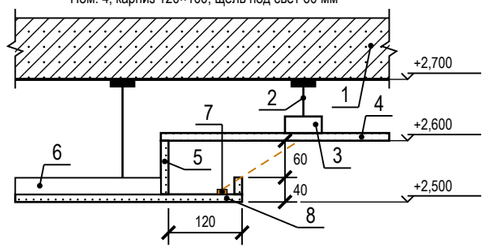


1 — плита перекрытия
2 — подвес прямой, шаг 1000 мм
3 — ПП 60×27: несущие через 500, основные через 1200 мм
4 — ГКЛ 12,5 по П113 — верхний уровень
5 — задняя стенка и бортик карниза — ГКЛ 12,5
6 — ПП 60×27 каркаса нижнего уровня, ПН по контуру фигуры (на дуге — с надрезами)
7 — LED-лента в алюминиевом профиле
8 — низ короба — ГКЛ 12,5 по ПП 60×27

### Условные обозначения

— · — LED-лента в нише подсветки (карниз короба, ниша фигуры)


### Примечания

1. ГКЛ 12,5 мм по каркасу П113; узлы коробов и ниш под шторы: узел 1 — лист 58; узел 2 — лист 58; узел 5 — на этом листе; узел 4 — лист 59; узел 3 — лист 58.

| | | | | | | |
|---|---|---|---|---|---|---|
| | | | | | Проект: Квартира с кабинетом | М 1:10 |
| | Лист | № док. | Подпись | Дата | | |
| Дизайнер | Кырлан А.С. | | | 04.11.26 | Разрезы и узлы потолков (продолжение) | Стадия: П; Лист: 60; Листов: 127 |

## Сечение 1.1. Короб с LED-подсветкой (М 1:10)


Пом. 1 Спальня; карниз 150×100, щель под свет 60 мм

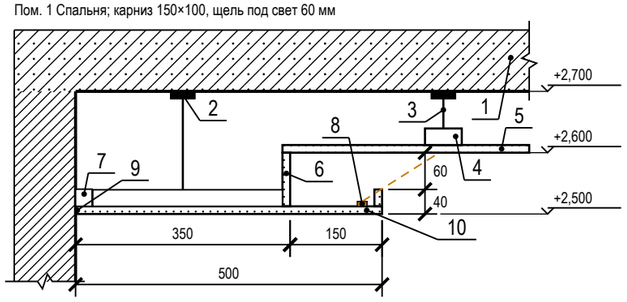


1 — плита перекрытия
2 — анкер-клин к плите — по одному на подвес
3 — подвес прямой, шаг 1000 мм
4 — ПП 60×27: несущие через 500, основные через 1200 мм; соединители одноуровневые, шурупы LN 3,5×9
5 — ГКЛ 12,5 по П113 — верхний уровень; шурупы TN 3,5×25 через 170 мм
6 — задняя стенка и бортик карниза — ГКЛ 12,5
7 — ПН 28×27 по периметру — дюбель-гвоздь через ≤ 500 мм, не менее 3 на профиль
8 — LED-лента 9,6 Вт/м, 24 В в алюминиевом профиле
9 — примыкание к стене — лента разделительная, шов зашпаклёван
10 — низ короба — ГКЛ 12,5 по ПП 60×27

## Сечение 1.2. Ниша под шторы (М 1:10)


Пом. 1 Спальня; без подсветки; закладные под карниз — до обшивки

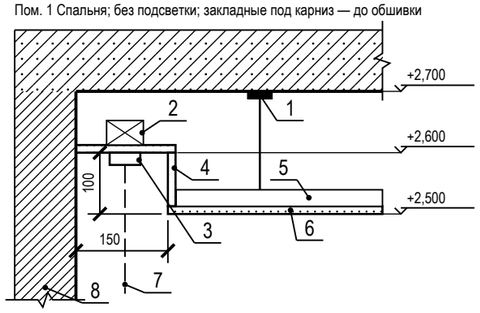


1 — анкер-клин к плите — по одному на подвес; подвес прямой, шаг 1000 мм
2 — закладная под карниз — брус 40×50
3 — карниз (шина), высота с верхом портьеры 80 мм
4 — стенка и потолок ниши — ГКЛ 12,5
5 — ПП 60×27 — каркас короба, основные через 1200 мм; соединители одноуровневые, шурупы LN 3,5×9
6 — низ короба нижнего уровня — ГКЛ 12,5; шурупы TN 3,5×25 через 170 мм
7 — портьера
8 — стена с окном

## Сечение 3.1. Короб с LED-подсветкой (М 1:10)


Пом. 3 Кабинет; карниз 150×100, щель под свет 60 мм

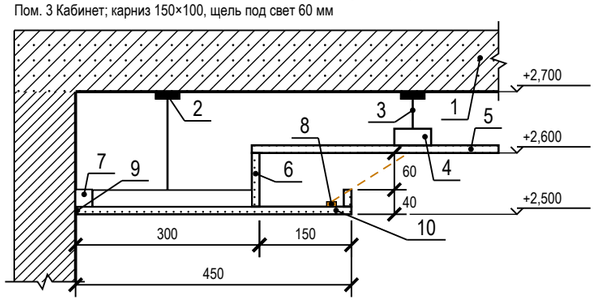


1 — плита перекрытия
2 — анкер-клин к плите — по одному на подвес
3 — подвес прямой, шаг 1000 мм
4 — ПП 60×27: несущие через 500, основные через 1200 мм; соединители одноуровневые, шурупы LN 3,5×9
5 — ГКЛ 12,5 по П113 — верхний уровень; шурупы TN 3,5×25 через 170 мм
6 — задняя стенка и бортик карниза — ГКЛ 12,5
7 — ПН 28×27 по периметру — дюбель-гвоздь через ≤ 500 мм, не менее 3 на профиль
8 — LED-лента 9,6 Вт/м, 24 В в алюминиевом профиле
9 — примыкание к стене — лента разделительная, шов зашпаклёван
10 — низ короба — ГКЛ 12,5 по ПП 60×27

## Сечение 3.2. Ниша под шторы (М 1:10)


Пом. 3 Кабинет; без подсветки; закладные под карниз — до обшивки

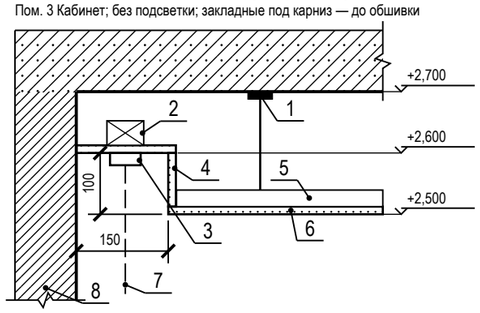


1 — анкер-клин к плите — по одному на подвес; подвес прямой, шаг 1000 мм
2 — закладная под карниз — брус 40×50
3 — карниз (шина), высота с верхом портьеры 80 мм
4 — стенка и потолок ниши — ГКЛ 12,5
5 — ПП 60×27 — каркас короба, основные через 1200 мм; соединители одноуровневые, шурупы LN 3,5×9
6 — низ короба нижнего уровня — ГКЛ 12,5; шурупы TN 3,5×25 через 170 мм
7 — портьера
8 — стена с окном

## Сечение 4.1. Ниша LED фигурного уровня (М 1:10)


Пом. 4 Кухня-гостиная; карниз 120×100, щель под свет 60 мм

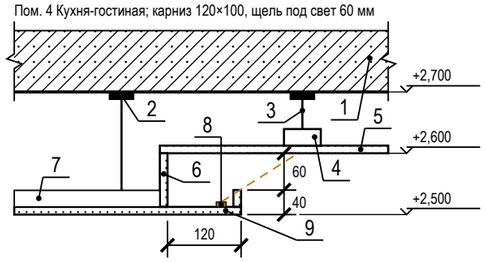


1 — плита перекрытия
2 — анкер-клин к плите — по одному на подвес
3 — подвес прямой, шаг 1000 мм
4 — ПП 60×27: несущие через 500, основные через 1200 мм; соединители одноуровневые, шурупы LN 3,5×9
5 — ГКЛ 12,5 по П113 — верхний уровень; шурупы TN 3,5×25 через 170 мм
6 — задняя стенка и бортик карниза — ГКЛ 12,5
7 — ПП 60×27 каркаса нижнего уровня, ПН по контуру фигуры (на дуге — с надрезами)
8 — LED-лента 9,6 Вт/м, 24 В в алюминиевом профиле
9 — низ короба — ГКЛ 12,5 по ПП 60×27

## Сечение 4.2. Ниша под шторы (М 1:10)

Пом. 4 Кухня-гостиная; без подсветки; закладные под карниз — до обшивки

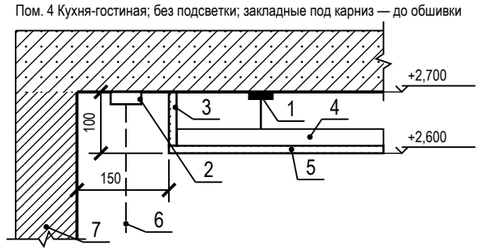


1 — анкер-клин к плите — по одному на подвес; подвес прямой, шаг 1000 мм
2 — карниз (шина), высота с верхом портьеры 80 мм
3 — стенка ниши — ГКЛ 12,5
4 — ПП 60×27 — каркас короба, основные через 1200 мм; соединители одноуровневые, шурупы LN 3,5×9
5 — низ короба нижнего уровня — ГКЛ 12,5; шурупы TN 3,5×25 через 170 мм
6 — портьера
7 — стена с окном

## Условные обозначения

— · — LED-лента в нише подсветки (карниз короба, ниша фигуры)

## Примечания

1. Сечения потолков М 1:10 по помещениям с нишами LED и нишами под шторы: отметки и размеры этого помещения от ±0,000 чистого пола (м, мм). Положение — по плану потолков (лист 57): короб и ниша LED — по линиям ленты, ниша под шторы — у стены с окном; типовые узлы по группам помещений — на листе 58.
2. Крепёж: подвес прямой к плите на анкер-клине — по одному на подвес (Knauf П113); ПН к стенам — дюбель-гвоздь через ≤ 500 мм, не менее 3 на профиль (серия 1.045.9-2.08); лист 12,5 — шурупы TN 3,5×25 через 170 мм (СП 163, табл. 15); профили между собой — соединители одноуровневые, шурупы LN 3,5×9.
3. Изделие карниза, профиля LED и галтели подписано артикулом из данных; где артикул не выбран, сечение дано по габаритам из данных (ширина и глубина ниши, щель под свет), изделие подбирается по ним.

| | | | | | | |
|---|---|---|---|---|---|---|
| | | | | | Проект: Квартира с кабинетом | М 1:10 |
| | Лист | № док. | Подпись | Дата | Сечения потолков М 1:10 | Стадия / Лист / Листов |
| Дизайнер | Кырлан А.С. | | | 04.11.26 | | П / 61 / 127 |

## Сечение 4.3. Примыкание потолка к стене (М 1:10)


Пом. 4 Кухня-гостиная; примыкание — разделительная лента




1 — плита перекрытия
2 — анкер-клин к плите — по одному на подвес
3 — подвес прямой, шаг 1000 мм
4 — ПН 28×27 по периметру — дюбель-гвоздь через ≤ 500 мм, не менее 3 на профиль
5 — ПП 60×27 несущий (вид) через 500 мм, в ПН
6 — ПП 60×27 основной (сечение) через 1200 мм; соединители одноуровневые, шурупы LN 3,5×9
7 — лента разделительная по стене, шов зашпаклёван
8 — ГКЛ 12,5 по П113; шурупы TN 3,5×25 через 170 мм

## Сечение 6.1. Короб с LED-подсветкой (М 1:10)


Пом. 6 Детская; карниз 150×100, щель под свет 60 мм

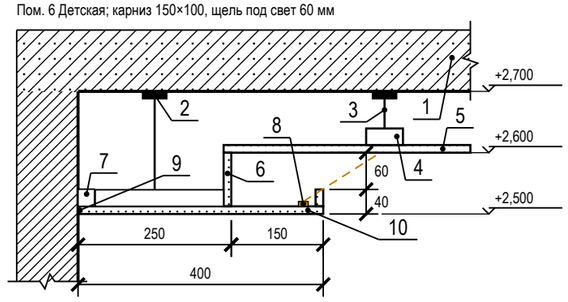


1 — плита перекрытия
2 — анкер-клин к плите — по одному на подвес
3 — подвес прямой, шаг 1000 мм
4 — ПП 60×27: несущие через 500, основные через 1200 мм; соединители одноуровневые, шурупы LN 3,5×9
5 — ГКЛ 12,5 по П113 — верхний уровень; шурупы TN 3,5×25 через 170 мм
6 — задняя стенка и бортик карниза — ГКЛ 12,5
7 — ПН 28×27 по периметру — дюбель-гвоздь через ≤ 500 мм, не менее 3 на профиль
8 — LED-лента 9,6 Вт/м, 24 В в алюминиевом профиле
9 — примыкание к стене — лента разделительная, шов зашпаклёван
10 — низ короба — ГКЛ 12,5 по ПП 60×27

## Сечение 6.2. Ниша под шторы (М 1:10)

Пом. 6 Детская; без подсветки; закладные под карниз — до обшивки

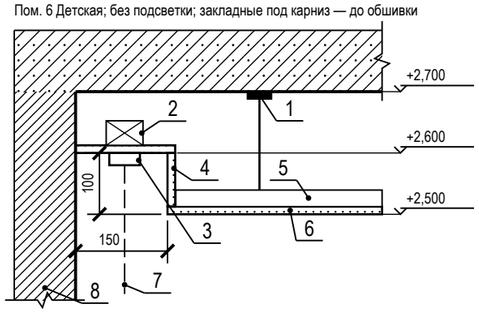


1 — анкер-клин к плите — по одному на подвес; подвес прямой, шаг 1000 мм
2 — закладная под карниз — брус 40×50
3 — карниз (шина), высота с верхом портьеры 80 мм
4 — стенка и потолок ниши — ГКЛ 12,5
5 — ПП 60×27 — каркас короба, основные через 1200 мм; соединители одноуровневые, шурупы LN 3,5×9
6 — низ короба нижнего уровня — ГКЛ 12,5; шурупы TN 3,5×25 через 170 мм
7 — портьера
8 — стена с окном

## Условные обозначения


— · — LED-лента в нише подсветки (карниз короба, ниша фигуры)

## Примечания

1. Сечения потолков М 1:10 по помещениям с нишами LED и нишами под шторы: отметки и размеры этого помещения от ±0,000 чистого пола (м, мм). Положение — по плану потолков (лист 57): короб и ниша LED — по линиям ленты, ниша под шторы — у стены с окном; типовые узлы по группам помещений — на листе 58.
2. Крепёж: подвес прямой к плите на анкер-клине — по одному на подвес (Knauf П113); ПН к стенам — дюбель-гвоздь через ≤ 500 мм, не менее 3 на профиль (серия 1.045.9-2.08); лист 12,5 — шурупы TN 3,5×25 через 170 мм (СП 163, табл. 15); профили между собой — соединители одноуровневые, шурупы LN 3,5×9.
3. Изделие карниза, профиля LED и галтели подписано артикулом из данных; где артикул не выбран, сечение дано по габаритам из данных (ширина и глубина ниши, щель под свет), изделие подбирается по ним.

| | | | | | | |
|---|---|---|---|---|---|---|
| | | | | | Проект: Квартира с кабинетом | М 1:10 |
| | Лист | № док. | Подпись | Дата | | |
| Дизайнер | Кырлан А.С. | | | 04.11.26 | Сечения потолков М 1:10 | Стадия: П; Лист: 62; Листов: 127 |

выпуск 04.11.2026 № 627e1ac6ce · стр. 62 из 127

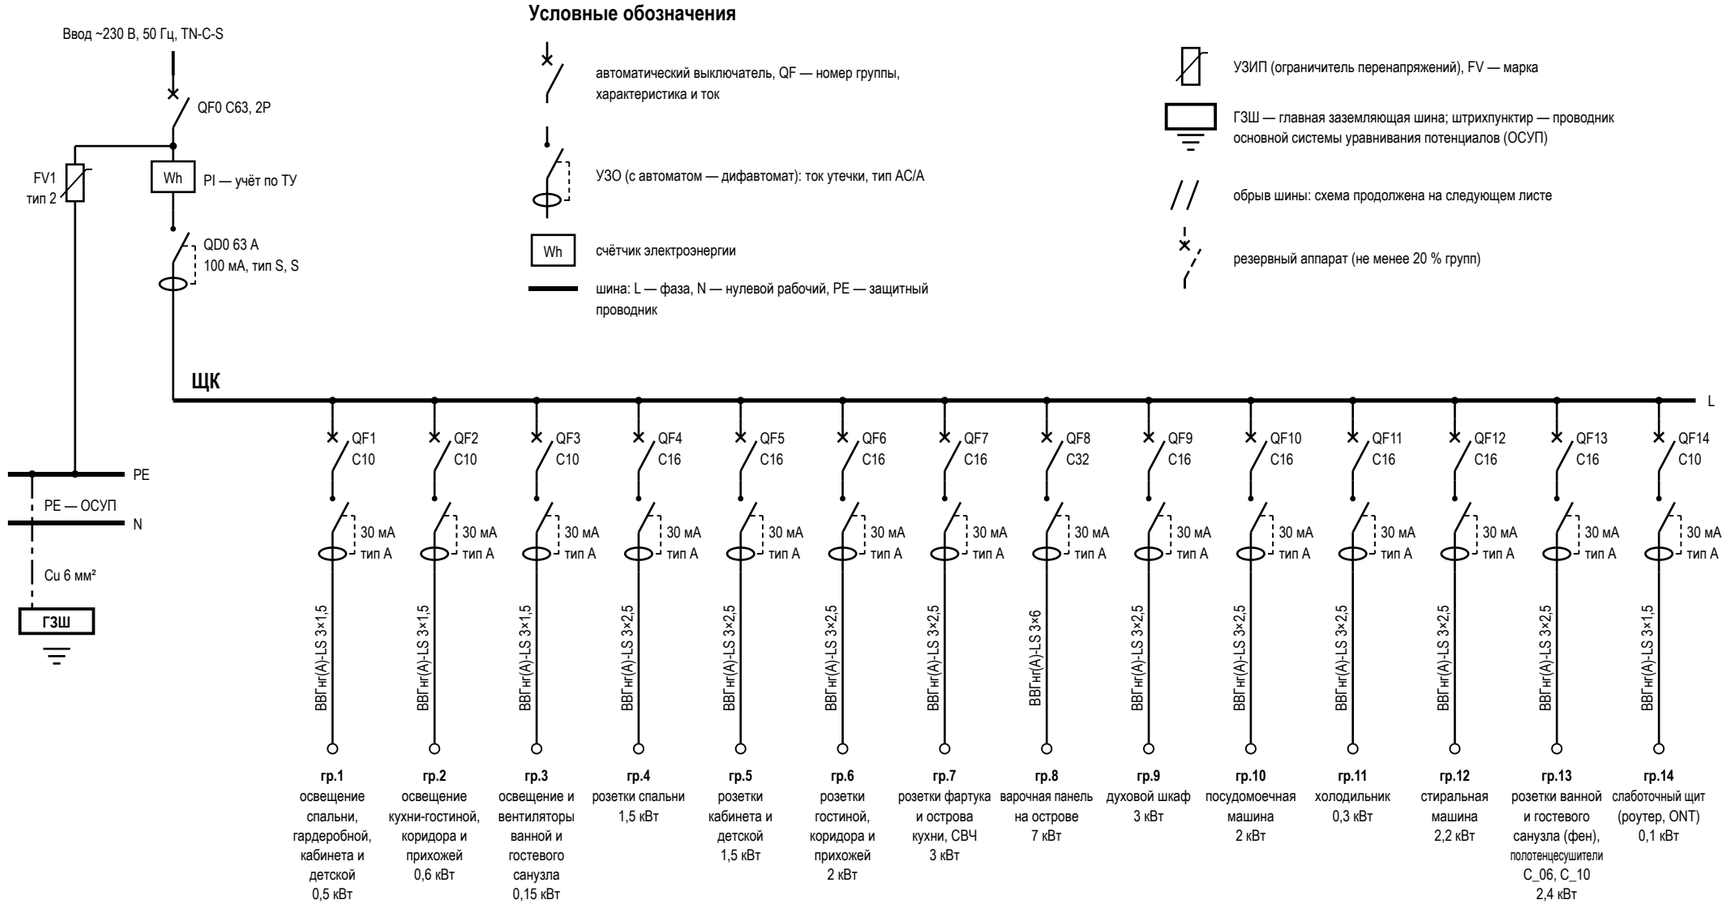


## Условные обозначения

- автоматический выключатель, QF — номер группы, характеристика и ток
- УЗО (с автоматом — дифавтомат): ток утечки, тип AC/A
- Wh — счётчик электроэнергии
- шина: L — фаза, N — нулевой рабочий, PE — защитный проводник
- УЗИП (ограничитель перенапряжений), FV — марка
- ГЗШ — главная заземляющая шина; штрихпунктир — проводник основной системы уравнивания потенциалов (ОСУП)
- обрыв шины: схема продолжена на следующем листе
- резервный аппарат (не менее 20 % групп)

## Данные щитка

| Показатель | Значение |
|---|---|
| Номер щитка | ЩК |
| Тип | ЩРВ-П-48, IP41 |
| Уст. мощность, кВт | 26,25 |
| Разреш. мощность, кВт | 15 |
| Расчётная, кВт | 9,8 |
| Автоматы 1п: занят. / рез. | 14 / 3 |
| Модулей: всего / занято | 48 / 34 |
| Ток на вводе, А | 63 |
| Вводной аппарат | QF0 C63, 2P |
| УЗИП | FV1, тип 2, ЩК, после счётчика |
| ГЗШ, проводник ОСУП | Cu 6 мм² |
| Листов схемы | 2 (группы по листам) |

## Таблица групп щита ЩК и кабельный журнал


| № | Назначение | Помещения | Автомат | УЗО / дифавтомат | Кабель | Длина, м | P, кВт | Точек |
|---|---|---|---|---|---|---|---|---|
| 1 | освещение спальни, гардеробной, кабинета и детской | 1, 2, 3, 5, 6 | C10 | 30 мА, тип A | ВВГнг(A)-LS 3×1,5 | 123,1 | 0,5 | 41 |
| 2 | освещение кухни-гостиной, коридора и прихожей | 4, 5, 8 | C10 | 30 мА, тип A | ВВГнг(A)-LS 3×1,5 | 87 | 0,6 | 37 |
| 3 | освещение и вентиляторы ванной и гостевого санузла | 5, 7, 8, 9 | C10 | 30 мА, тип A | ВВГнг(A)-LS 3×1,5 | 35 | 0,15 | 11 |
| 4 | розетки спальни | 1 | C16 | 30 мА, тип A | ВВГнг(A)-LS 3×2,5 | 40,2 | 1,5 | 6 |
| 5 | розетки кабинета и детской | 3, 6 | C16 | 30 мА, тип A | ВВГнг(A)-LS 3×2,5 | 44,8 | 1,5 | 10 |
| 6 | розетки гостиной, коридора и прихожей | 4, 5, 8 | C16 | 30 мА, тип A | ВВГнг(A)-LS 3×2,5 | 49 | 2 | 8 |
| 7 | розетки фартука и острова кухни, СВЧ | 4 | C16 | 30 мА, тип A | ВВГнг(A)-LS 3×2,5 | 30,7 | 3 | 5 |
| 8 | варочная панель на острове | 4 | C32 | 30 мА, тип A | ВВГнг(A)-LS 3×6 | 12,4 | 7 | 1 |
| 9 | духовой шкаф | 4 | C16 | 30 мА, тип A | ВВГнг(A)-LS 3×2,5 | 17,8 | 3 | 1 |
| 10 | посудомоечная машина | 4 | C16 | 30 мА, тип A | ВВГнг(A)-LS 3×2,5 | 17,4 | 2 | 1 |
| 11 | холодильник | 4 | C16 | 30 мА, тип A | ВВГнг(A)-LS 3×2,5 | 14,4 | 0,3 | 1 |
| 12 | стиральная машина | 7 | C16 | 30 мА, тип A | ВВГнг(A)-LS 3×2,5 | 15,2 | 2,2 | 1 |
| 13 | розетки ванной и гостевого санузла (фен), полотенцесушители C_06, C_10 | 7, 9 | C16 | 30 мА, тип A | ВВГнг(A)-LS 3×2,5 | 31,2 | 2,4 | 4 |
| 14 | слаботочный щит (роутер, ONT) | 8 | C10 | 30 мА, тип A | ВВГнг(A)-LS 3×1,5 | 3,5 | 0,1 | 1 |
| | Итого по сечениям ВВГнг(A)-LS (все группы щита), м: 3×1,5 — 248,6; 3×2,5 — 260,7; 3×6 — 12,4 | | | | | 521,7 | | |

## Примечания

1. Схема однолинейная: одна линия — фаза, N и PE группы; аппараты — в отключённом положении (ГОСТ 2.702, ГОСТ 2.755). Номера групп — как у точек на планах (гр.). За отметку 0,000 принят уровень чистого пола; высота щита — по плану розеток.
2. Розеточные и мокрые линии — через УЗО или дифавтомат с током утечки не более 30 мА (ПУЭ 7.1.79); в санузле выполнить ДСУП (ПУЭ 7.1.87–7.1.88).
3. УЗО тип A — для линий с электроникой, стиральной и посудомоечной машиной, LED-драйверами; тип AC — только для чисто активной нагрузки.
4. Кабель — медный, исполнение нг(A)-LS (ГОСТ 31565-2012); скрытая прокладка только горизонтально и вертикально, фактические трассы зафиксировать исполнительной схемой до закрытия отделкой.
5. Номинал автомата — не выше допустимого тока кабеля: 1,5 мм² — до 10 А, 2,5 мм² — до 16 А. Резерв щита — не менее 20 % модулей.
6. Расчёт нагрузок, токов КЗ, селективности и сечений — по проекту ЭОМ организации с допуском СРО; лист задаёт состав, расположение и группы.
7. УЗИП FV1 — после вводного автомата, проводник к шине PE — кратчайший, без петель. Шина PE щита соединяется с ГЗШ проводником ОСУП; к ГЗШ присоединяются трубы водопровода и отопления на вводе в квартиру (ПУЭ 7.1.87). Шины N и PE — раздельные, после разделения PEN не объединяются.
8. До подключения нагрузки — приёмо-сдаточные испытания с протоколом: сопротивление изоляции линий не менее 0,5 МОм, срабатывание УЗО по току и времени, непрерывность защитных проводников PE (ПУЭ, гл. 1.8).

| | | | | | |
|---|---|---|---|---|---|
| | | | | | Проект: Квартира с кабинетом |
| | Лист | № док. | Подпись | Дата | |
| Дизайнер | Кырлан А.С. | | | 04.11.26 | Однолинейная схема щита |
| | | | | | Стадия: П; Лист: 63; Листов: 127 |


Продолжение однолинейной схемы щита ЩК, начало — лист 63

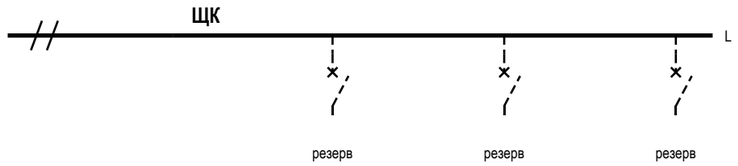


## Примечания

1. Лист — продолжение однолинейной схемы щита ЩК: начало, данные щитка и условные обозначения — лист 63. Ввод, учёт, вводной аппарат, УЗИП, шины N и PE и ГЗШ показаны там же; шина L листа — та же шина щита.
2. Схема однолинейная: одна линия — фаза, N и PE группы; аппараты — в отключённом положении (ГОСТ 2.702, ГОСТ 2.755). Номера групп — как у точек на планах (гр.). За отметку 0,000 принят уровень чистого пола; высота щита — по плану розеток.
3. Розеточные и мокрые линии — через УЗО или дифавтомат с током утечки не более 30 мА (ПУЭ 7.1.79); в санузле выполнить ДСУП (ПУЭ 7.1.87–7.1.88).
4. УЗО тип A — для линий с электроникой, стиральной и посудомоечной машиной, LED-драйверами; тип AC — только для чисто активной нагрузки.
5. Кабель — медный, исполнение нг(A)-LS (ГОСТ 31565-2012); скрытая прокладка только горизонтально и вертикально, фактические трассы зафиксировать исполнительной схемой до закрытия отделкой.
6. Номинал автомата — не выше допустимого тока кабеля: 1,5 мм² — до 10 А, 2,5 мм² — до 16 А. Резерв щита — не менее 20 % модулей.
7. Расчёт нагрузок, токов КЗ, селективности и сечений — по проекту ЭОМ организации с допуском СРО; лист задаёт состав, расположение и группы.
8. До подключения нагрузки — приёмо-сдаточные испытания с протоколом: сопротивление изоляции линий не менее 0,5 МОм, срабатывание УЗО по току и времени, непрерывность защитных проводников PE (ПУЭ, гл. 1.8).

| | | | | | | | |
|---|---|---|---|---|---|---|---|
| | | | | | Проект: Квартира с кабинетом | | |
| | Лист | № док. | Подпись | Дата | Однолинейная схема щита (продолжение) | Стадия | Лист | Листов |
| Дизайнер | Кырлан А.С. | | | 04.11.26 | | П | 64 | 127 |

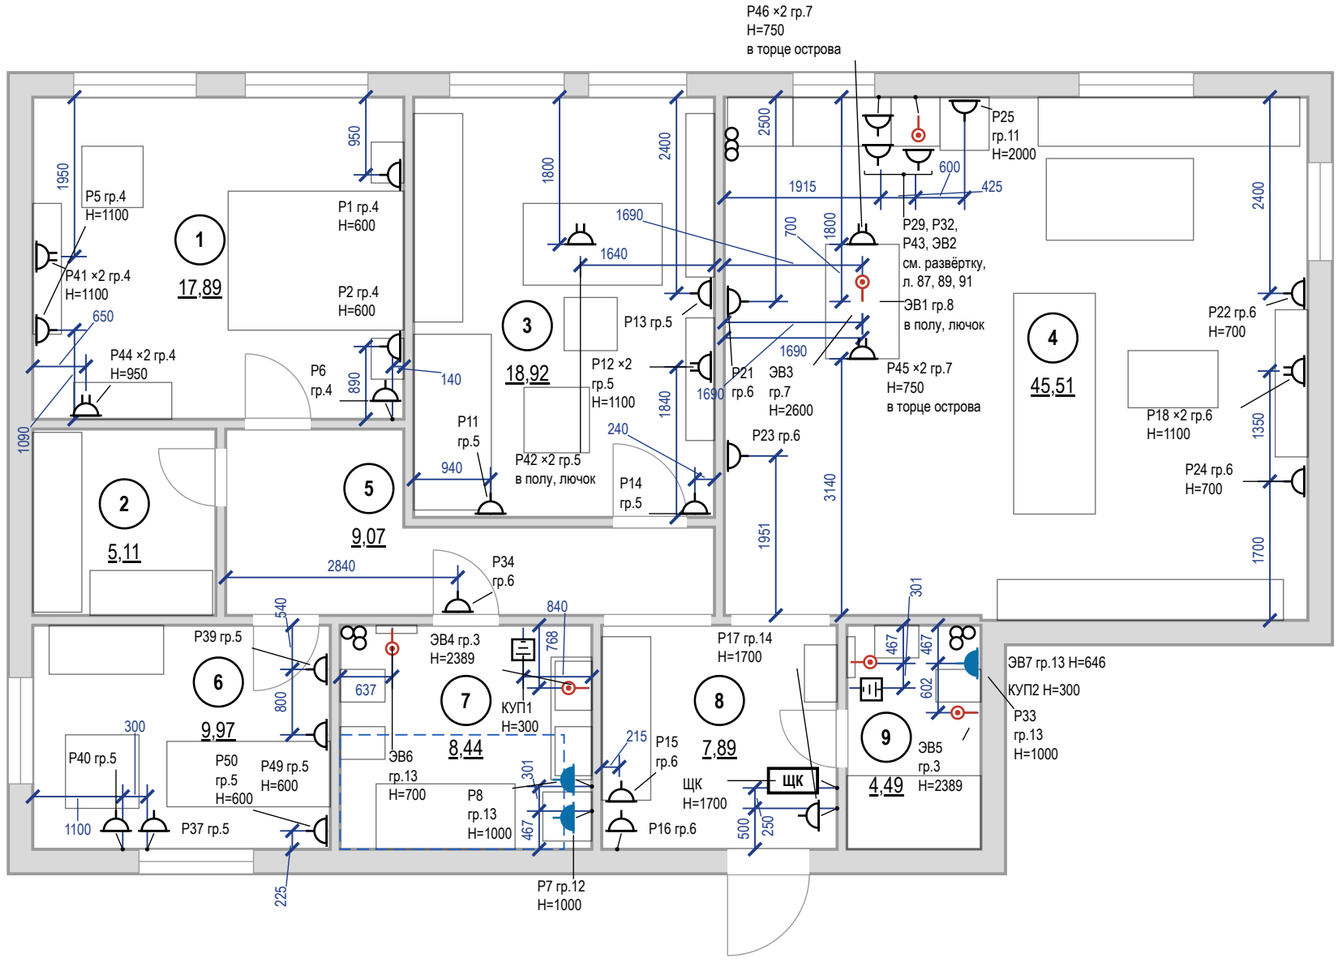


## Условные обозначения

| Знак | Тип изделия | Н, мм | Кол., шт |
|---|---|---|---|
| | Розетка с заземлением | 300 | 13 |
| | То же | у знака | 11 |
| | Блок розеток с заземлением, рамка 2 поста | у знака | 7 |
| | Розетка с заземлением IP44 | 1000 | 3 |
| | Вывод кабеля к прибору | у знака | 7 |
| | КУП (уравнивание потенциалов) | 300 | 2 |
| ЩК | Щит квартирный | 1700 | 1 |

розетка с заземляющим контактом; у знака — марка, ×N — постов в рамке, гр. — группа щита, Н — высота оси, мм

знак разведён для читаемости: точка на стене — у выноски, привязка — до неё

граница зоны 2 ванной (600 мм от ванны/поддона)

мебель и сантехприборы — подложка

стояк: К1 — канализация, В1 — ХВС, Т3 — ГВС


1 — номер помещения, площадь м²

**Итого розеток (механизмов) — 41 шт; рамок — 34 шт: на 1 пост — 27, на 2 поста — 7.**

## Примечания

1. За отметку 0,000 принят уровень чистого пола. Высоты Н — от чистого пола до оси изделия; привязки — от чистовой грани стены до оси механизма (у рамки на несколько постов — до оси рамки).
2. Розетки без отметки Н у знака — на высоте 300 мм от чистого пола до оси механизма; выводы кабеля — по паспорту прибора.
3. Розетки в санузле — только вне зон 0–2 (ПУЭ 7.1.48, ГОСТ Р 50571.7.701-2024), IP44, через УЗО 30 мА.
4. Розеточные и мокрые линии — через УЗО или дифавтомат с током утечки не более 30 мА (ПУЭ 7.1.79); в санузле выполнить ДСУП (ПУЭ 7.1.87–7.1.88).
5. Кабель — медный, исполнение нг(А)-LS (ГОСТ 31565-2012); скрытая прокладка только горизонтально и вертикально, фактические трассы зафиксировать исполнительной схемой до закрытия отделкой.
6. Расчёт нагрузок, токов КЗ, селективности и сечений — по проекту ЭОМ организации с допуском СРО; лист задаёт состав, расположение и группы.
7. Выводы кухонной техники — после утверждения проекта кухни (ориентировочно); привязки выводов даны от осей модулей гарнитура и пересматриваются вместе с проектом кухни.
8. Электрический тёплый пол проектом не предусмотрен; при решении заказчика устроить — отдельный лист «План тёплых полов»: контуры с отступом 100 мм от стен и мебели без ножек, датчик в гофре, терморегулятор, своя группа щита через УЗО 30 мА.

| | | | | | | |
|---|---|---|---|---|---|---|
| | | | | | Проект: Квартира с кабинетом | М 1:75 |
| | Лист | № док. | Подпись | Дата | | |
| Дизайнер | Кырлан А.С. | | | 04.11.26 | План розеток и электровыводов | Стадия: П; Лист: 65; Листов: 127 |

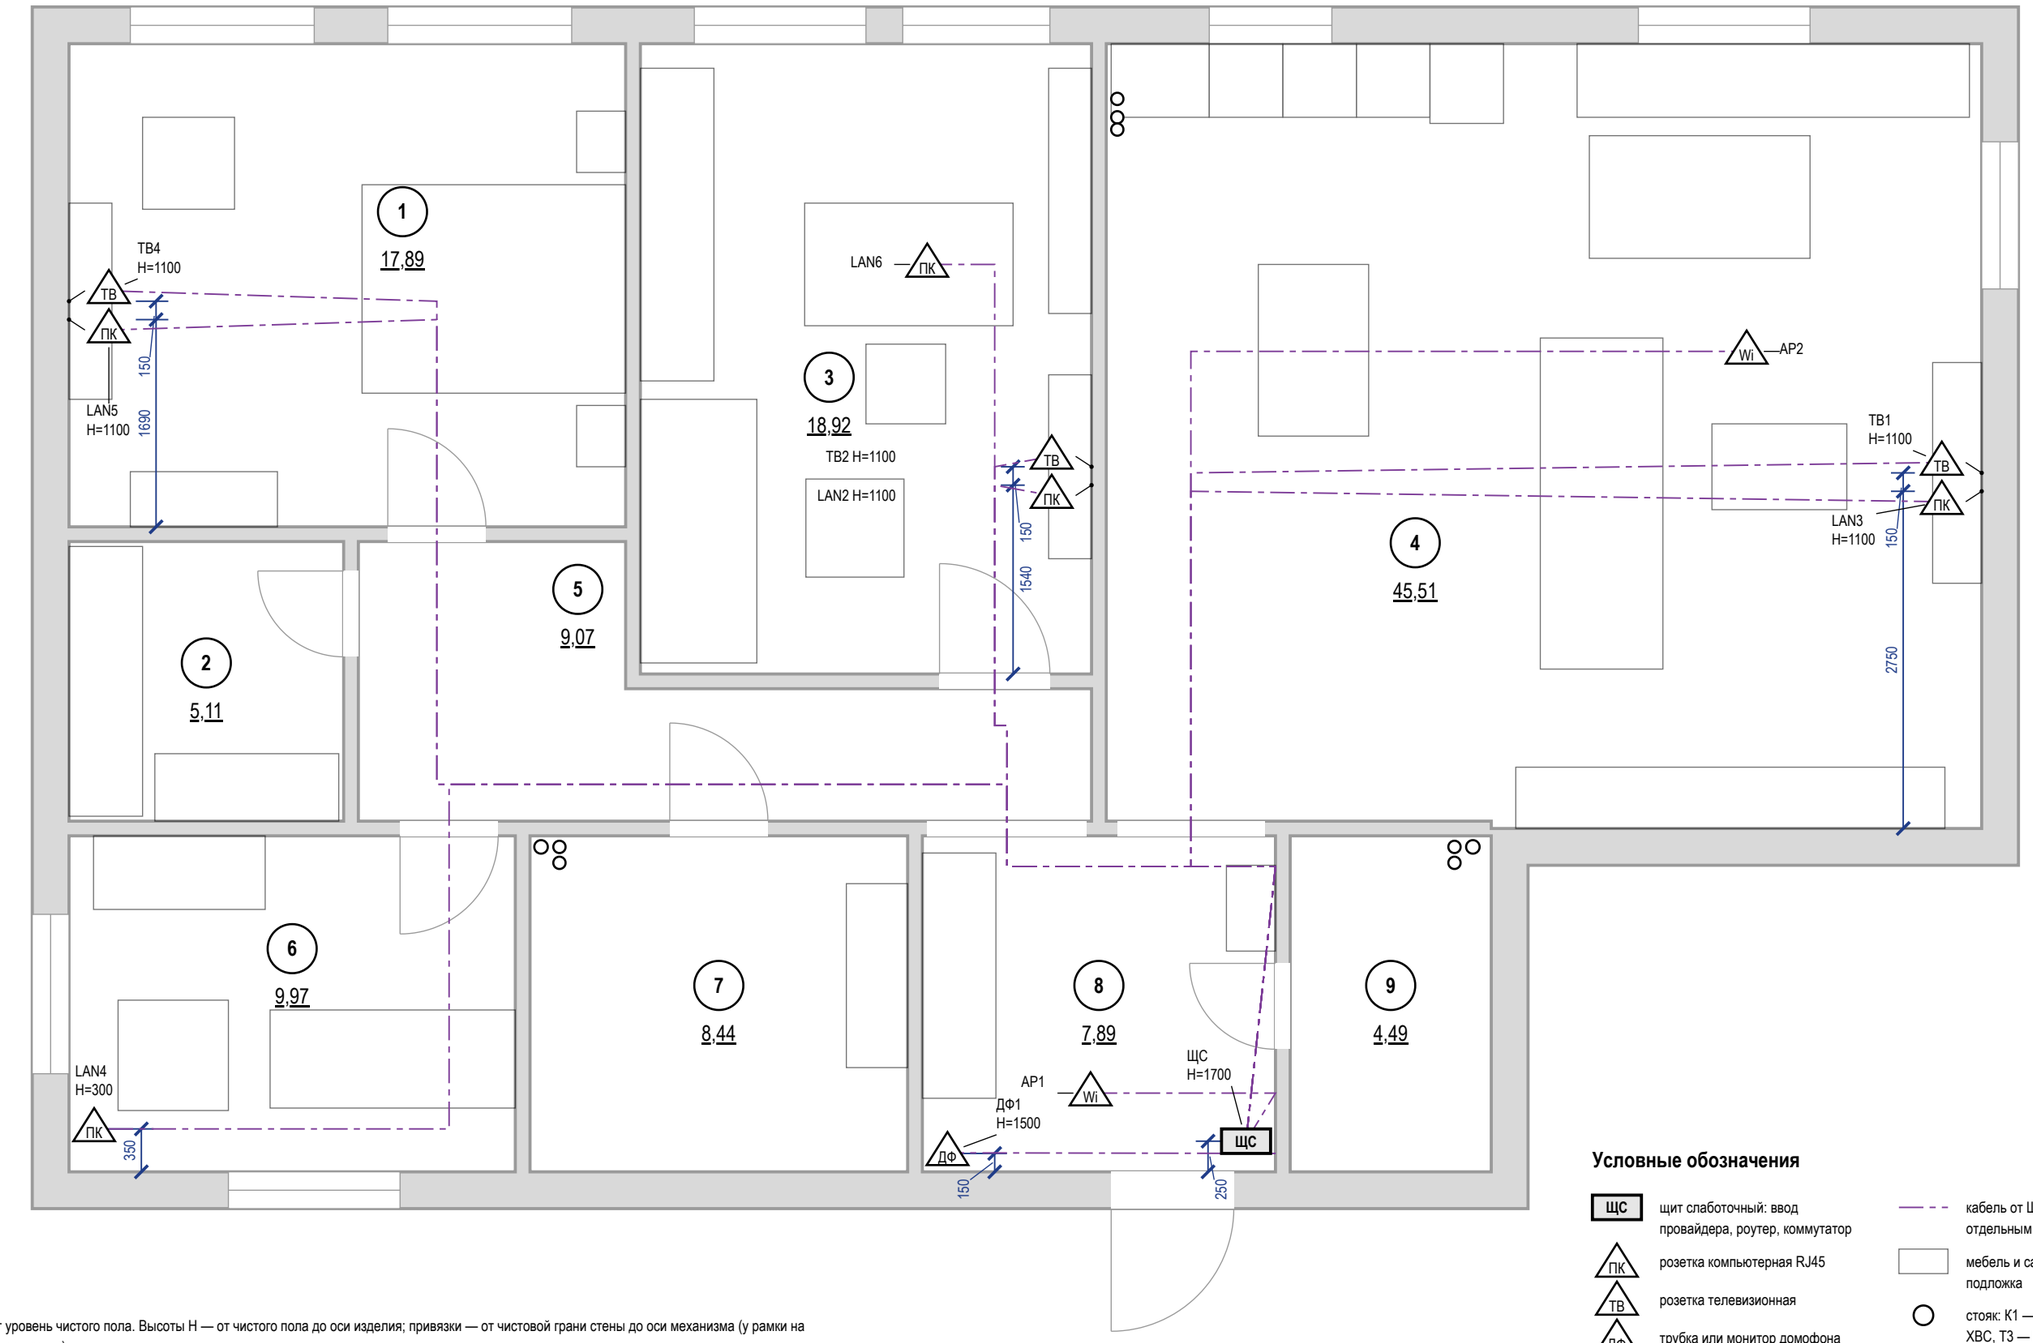



## Примечания

1. За отметку 0,000 принят уровень чистого пола. Высоты Н — от чистого пола до оси изделия; привязки — от чистовой грани стены до оси механизма (у рамки на несколько постов — до оси рамки).
2. Высота установки, не указанная на плане: розетки LAN и ТВ — 300 мм от чистого пола.
3. Слаботочные кабели — отдельно от силовых: в своей трубе или лотке, при параллельной прокладке не ближе 100 мм к силовым, пересечения под прямым углом; каждую точку — отдельным кабелем от ЩС без скруток.
4. Трассы на листе — принципиальные; фактические зафиксировать исполнительной схемой до закрытия отделкой. Силовые линии, УЗО 30 мА, ДСУП, кабель нг(А)-LS — по листам розеток и щита.
5. Проект силовой части и расчёт токов КЗ — по проекту ЭОМ; слаботочная часть согласуется с провайдером и управляющей компанией (домофон, коллективное ТВ).

## Условные обозначения

- ЩС — щит слаботочный: ввод провайдера, роутер, коммутатор
- ПК — розетка компьютерная RJ45
- ТВ — розетка телевизионная
- ДФ — трубка или монитор домофона
- Wi — точка доступа Wi-Fi (питание PoE)
- кабель от ЩС до точки, отдельным лучом
- мебель и сантехприборы подложка
- стояк: К1 — канализация, В1 ХВС, Т3 — ГВС
- 1 — номер помещения, площадь м²

| | | | | | |
|---|---|---|---|---|---|
| | | | | | Проект: Квартира с кабинетом — М 1:50 |
| | Лист | № док. | Подпись | Дата | План слаботочных сетей |
| Дизайнер | Кырлан А.С. | | | 04.11.26 | Стадия: П; Лист: 66; Листов: 127 |

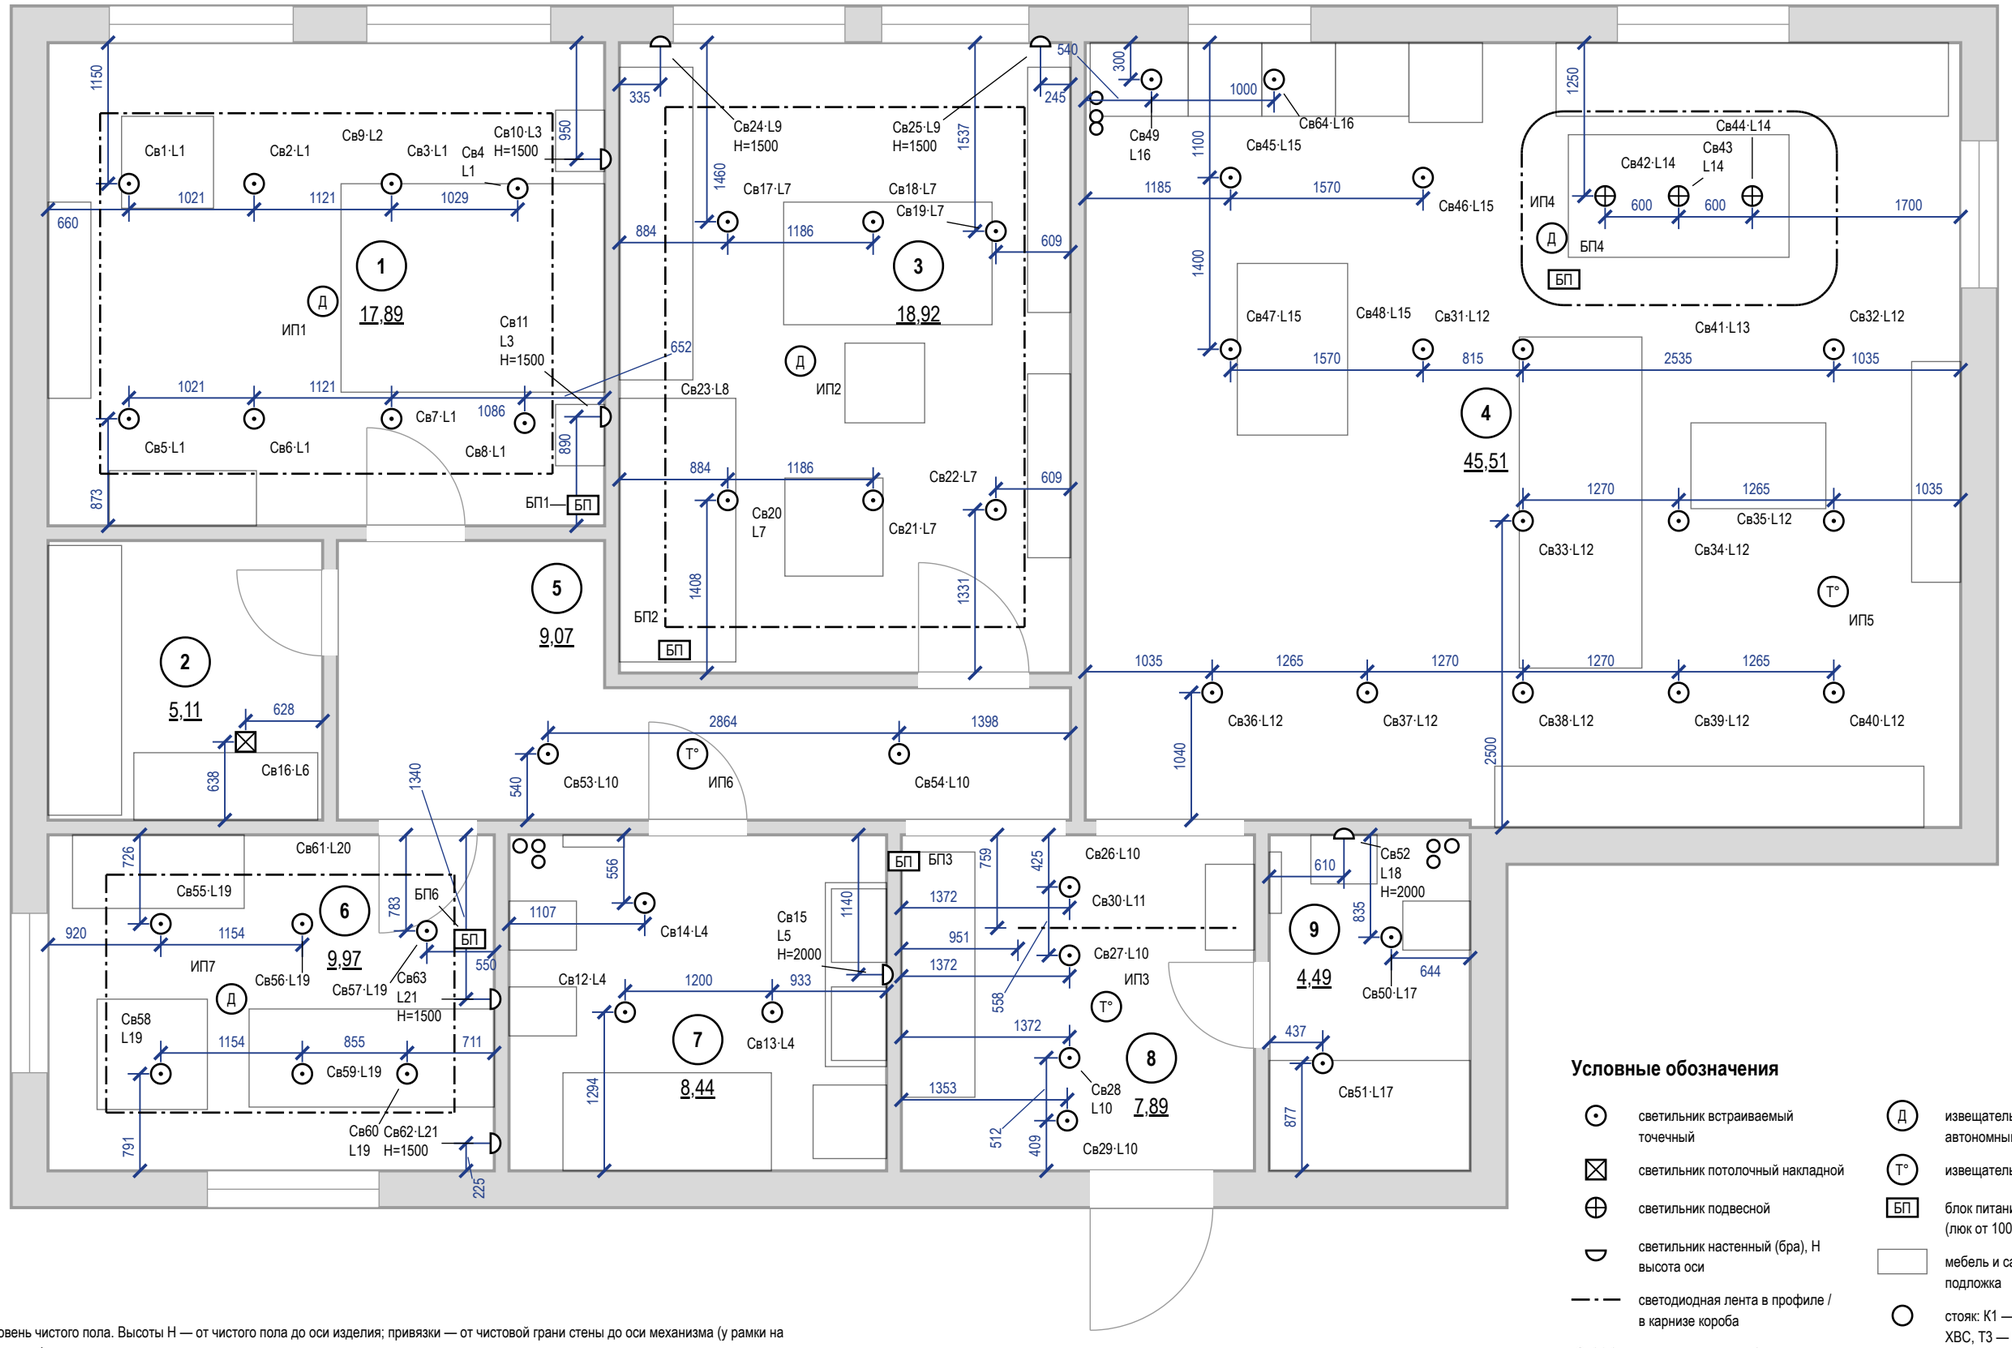


## Примечания

1. За отметку 0,000 принят уровень чистого пола. Высоты H — от чистого пола до оси изделия; привязки — от чистовой грани стены до оси механизма (у рамки на несколько постов — до оси рамки).
2. Высота установки, не указанная на плане: светильники — на потолке; настенные — по отметке H у знака. Привязки — до оси светильника от чистовой грани стены, по рядам.
3. Во влажных помещениях — светильники не ниже IP44; в зонах 0–2 ванной — по ГОСТ Р 50571.7.701-2024 (зона 1 — IPX5).
4. LED-лента в карнизе подсветки короба — по линии карниза с плана потолков; блок питания — в люке короба (БП на плане), питание ленты длиннее 5 м — с двух концов.
5. Розеточные и мокрые линии — через УЗО или дифавтомат с током утечки не более 30 мА (ПУЭ 7.1.79); в санузле выполнить ДСУП (ПУЭ 7.1.87–7.1.88).
6. Кабель — медный, исполнение нг(A)-LS (ГОСТ 31565-2012); скрытая прокладка только горизонтально и вертикально, фактические трассы зафиксировать исполнительной схемой до закрытия отделкой.
7. Расчёт нагрузок, токов КЗ, селективности и сечений — по проекту ЭОМ организации с допуском СРО; лист задаёт состав, расположение и группы.
8. Ведомость светильников (тип, количество, мощность, поток, Tц, Ra) — лист 68.

## Условные обозначения

- светильник встраиваемый точечный
- светильник потолочный накладной
- светильник подвесной
- светильник настенный (бра), H высота оси
- светодиодная лента в профиле / в карнизе короба
- Св1·L1 — марка светильника (как в ведомости и на развёртках) · группа включения L (лист 69)
- Д — извещатель пожарный дымовой автономный
- T° — извещатель пожарный тепловой
- БП — блок питания LED, с доступом (люк от 100×100 мм)
- мебель и сантехприборы подложка
- стояк: К1 — канализация, В1 ХВС, Т3 — ГВС
- 1 — номер помещения, площадь м²

| | | | | | |
|---|---|---|---|---|---|
| | | | | | Проект: Квартира с кабинетом — М 1:50 |
| | Лист | № док. | Подпись | Дата | |
| Дизайнер | Кырлан А.С. | | | 04.11.26 | План освещения |

| Стадия | Лист | Листов |
|---|---|---|
| П | 67 | 127 |

выпуск 04.11.2026 № 627e1ac6ce · стр. 67 из 127

## Параметры светильников для подбора

| Поз. | Марки | Наименование | Установка | Кол. | P, Вт | Σ P, Вт | Ф, лм | Тц, К | Ra | Угол, ° | IP | Дим. | Слой | Группа | Пом. |
|---|---|---|---|---|---|---|---|---|---|---|---|---|---|---|---|
| 1 | Св1–Св8 | Встраиваемый точечный | в ГКЛ, корпус ≤ 70 мм | 8 | 12 | 96 | 1000 | 2700 | 90 | — | 20 | — | общий | L1 | 1 |
| 2 | Св9 | Лента светодиодная 24 В | в карнизе короба, профиль с рассеивателем | 13,3 м | 9,6/м | 127,3 | 900/м | 2700 | 90 | — | 20 | да | акцентный | L2 | 1 |
| 3 | Св10, Св11, Св24, Св25, Св62, Св63 | Настенный (бра) | на стене, H=1500 | 6 | 6 | 36 | 400 | 2700 | 90 | 60 | 20 | — | рабочий | L3, L9, L21 | 1, 3, 6 |
| 4 | Св16 | Потолочный накладной | на потолке, засветка стены | 1 | 10 | 10 | 900 | 3000 | 90 | — | 20 | — | общий | L6 | 2 |
| 5 | Св17–Св22, Св55–Св60 | Встраиваемый точечный | в ГКЛ, корпус ≤ 70 мм | 12 | 12 | 144 | 1050 | 2700 | 90 | — | 20 | — | общий | L7, L19 | 3, 6 |
| 6 | Св23 | Лента светодиодная 24 В | в карнизе короба, профиль с рассеивателем | 14,3 м | 9,6/м | 137,7 | 900/м | 2700 | 90 | — | 20 | да | акцентный | L8 | 3 |
| 7 | Св31, Св32, Св33, Св34, Св35, Св36, Св37, Св38, Св39, Св40 | Встраиваемый точечный | в ГКЛ, корпус ≤ 70 мм | 10 | 12 | 120 | 1000 | 3000 | 90 | — | 20 | да | общий | L12 | 4 |
| 8 | Св41 | Лента светодиодная 24 В | в нише уровня, профиль с рассеивателем | 7,7 м | 9,6/м | 74,1 | 900/м | 2700 | 90 | — | 20 | да | акцентный | L13 | 4 |
| 9 | Св42, Св43, Св44 | Подвесной | подвес, низ H=1450 | 3 | 9 | 27 | 800 | 3000 | 90 | — | 20 | да | общий | L14 | 4 |
| 10 | Св45, Св46, Св47, Св48 | Встраиваемый точечный | в ГКЛ, корпус ≤ 70 мм | 4 | 10 | 40 | 900 | 3000 | 90 | — | 20 | — | общий | L15 | 4 |
| 11 | Св26–Св29, Св49, Св53, Св54, Св64 | Встраиваемый точечный | в ГКЛ, корпус ≤ 70 мм | 8 | 7 | 56 | 600 | 3000 | 90 | — | 20 | да | общий, рабочий | L10, L16 | 4, 5, 8 |
| 12 | Св61 | Лента светодиодная 24 В | в карнизе короба, профиль с рассеивателем | 9,6 м | 9,6/м | 91,8 | 900/м | 2700 | 90 | — | 20 | да | акцентный | L20 | 6 |
| 13 | Св12–Св14, Св51 | Встраиваемый точечный | в ГКЛ, корпус ≤ 70 мм | 4 | 6 | 24 | 500 | 3000 | 90 | — | 44 | — | общий | L4, L17 | 7, 9 |
| 14 | Св15, Св52 | Настенный светильник над зеркалом, драйвер встроен | над зеркалом, H=2000 | 2 | 8 | 16 | 600 | 3000 | 90 | — | 44 | — | рабочий | L5, L18 | 7, 9 |
| 15 | Св30 | Лента светодиодная 24 В | на поверхности, профиль с рассеивателем, датчик движения | 1,8 м | 4,8/м | 8,6 | 150/м | 2700 | 90 | — | 20 | нет | ночной | L11 | 8 |
| 16 | Св50 | Встраиваемый точечный | в ГКЛ, корпус ≤ 70 мм | 1 | 7 | 7 | 600 | 3000 | 90 | — | 44 | — | общий | L17 | 9 |
| | | **Итого** | | **59 шт + 46,7 м** | | **1015,5** | | | | | | | | | |

## LED-ленты, линейные светильники и блоки питания

| Марка | Пом. | L, м | U, В | Вт/м | Σ P, Вт | БП | P БП, Вт | Загр., % | Питание | Доступ к БП |
|---|---|---|---|---|---|---|---|---|---|---|
| Св9 | 1 | 13,3 | 24 | 9,6 | 127,3 | БП1 | 200 | 64 | с двух концов | люк 300×300 в коробе потолка ПТ1 |
| Св23 | 3 | 14,3 | 24 | 9,6 | 137,7 | БП2 | 200 | 69 | с двух концов | люк 300×300 в коробе потолка ПТ1 |
| Св41 | 4 | 7,7 | 24 | 9,6 | 74,1 | БП4 | 300 | 25 | с двух концов | люк 300×300 в нише фигуры потолка ПТ1 |
| Св61 | 6 | 9,6 | 24 | 9,6 | 91,8 | БП6 | 200 | 46 | с двух концов | люк 300×300 в коробе потолка ПТ1 |
| Св30 | 8 | 1,8 | 24 | 4,8 | 8,6 | БП3 | 20 | 43 | с одного конца | в шкафу M_30, верхняя полка |


## Сценарии (помещения со светорегуляторами)

| Помещение | Сценарий | Горят группы (уровень) | Управление |
|---|---|---|---|
| 4. Кухня-гостиная | Вечер | L12 споты гостиной — 30 %; L13 подсветка короба — 100 %; L14 подвесы над столом — 50 %; остальные выкл. | светорегуляторы S8, S9, S17 |
| | Ужин | L13 подсветка короба — 60 %; L14 подвесы над столом — 100 %; L16 подсветка столешницы — 30 %; остальные выкл. | светорегуляторы S9, S10, S17 |
| | Кино | L13 подсветка короба — 20 %; остальные выкл. | светорегулятор S17 |
| | Готовка | L12 споты гостиной — 50 %; L15 споты кухни — вкл.; L16 подсветка столешницы — 100 %; остальные выкл. | светорегуляторы S8, S10; выключатель S18 |

## Примечания

1. Позиции и марки Св — те же, что на плане освещения (лист 67); группы L — по плану выключателей (лист 69).
2. Модели светильников не выбраны: лист — техническое задание на подбор. Модель по строке таблицы: поток, Тц, Ra, угол, IP и регулировка яркости не хуже указанных, мощность не больше; встраиваемые — под глубину короба (графа «Установка»). IP 20 — сухие помещения. После выбора моделей (артикул, производитель) лист выпускается как «Спецификация светильников».
3. Длина LED-ленты в карнизе и нише уровня — по линиям карниза и ниши плана потолков (лист 57); Σ P = Вт/м × длина. Блок питания загружен не больше чем на 80 %; лента 24 В длиннее 10 м питается с двух концов; доступ к блоку питания — люк ревизии 300×300 мм или место, указанное в таблице.
4. Сценарии: % — яркость группы на светорегуляторе; «вкл.» — группа на обычной клавише; группы, не названные в строке, выключены. Светильники и блоки питания групп на светорегуляторе — с регулировкой яркости. Клавиши и светорегуляторы — лист 69.
5. В пом. 1, 3, 6 свет включается клавишами групп — лист 69.
6. Мощность и поток в таблице — требования к подбору (поток не меньше, мощность не больше указанных); после выбора модели — по её паспорту, Σ P — установленная мощность освещения. Оценка освещённости — на плане освещения; это не светотехнический расчёт.

| | | | | | |
|---|---|---|---|---|---|
| | | | | | Проект: Квартира с кабинетом |
| | Лист | № док. | Подпись | Дата | |
| Дизайнер | Кырлан А.С. | | | 04.11.26 | Техническое задание на подбор светильников |
| | | | | | Стадия: П; Лист: 68; Листов: 127 |

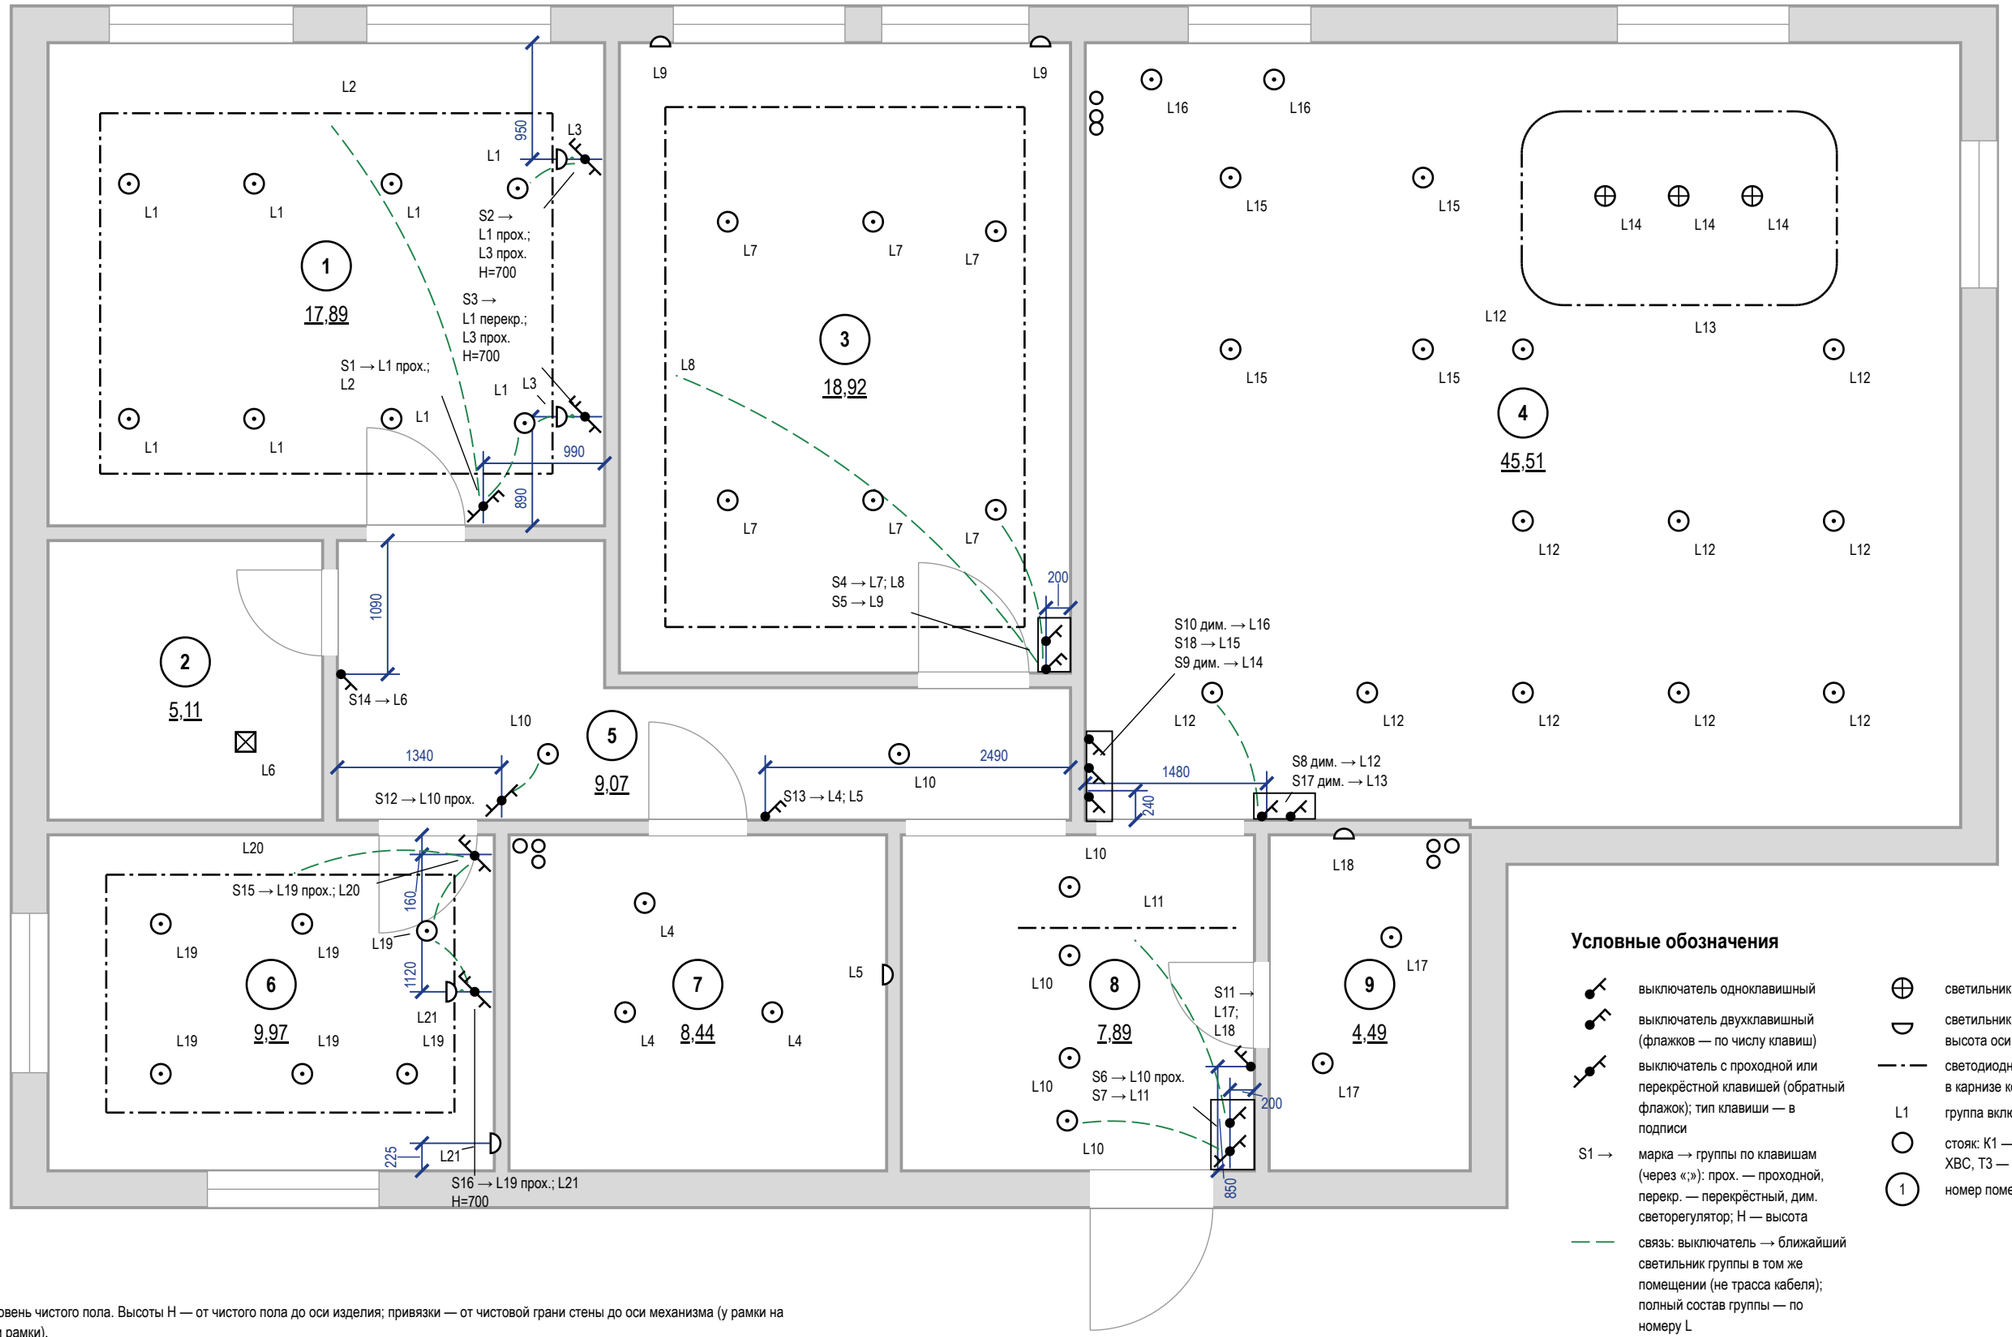



## Условные обозначения

- выключатель одноклавишный
- выключатель двухклавишный (флажков — по числу клавиш)
- выключатель с проходной или перекрёстной клавишей (обратный флажок); тип клавиши — в подписи
- S1 → — марка → группы по клавишам (через «;»): прох. — проходной, перекр. — перекрёстный, дим. светорегулятор; H — высота
- связь: выключатель → ближайший светильник группы в том же помещении (не трасса кабеля); полный состав группы — по номеру L
- светильник встраиваемый точечный
- светильник потолочный накладной
- светильник подвесной
- светильник настенный (бра), H высота оси
- светодиодная лента в профиле / в карнизе короба
- L1 — группа включения у светильника
- стояк: К1 — канализация, В1 ХВС, Т3 — ГВС
- 1 — номер помещения, площадь м²

## Примечания

1. За отметку 0,000 принят уровень чистого пола. Высоты H — от чистого пола до оси изделия; привязки — от чистовой грани стены до оси механизма (у рамки на несколько постов — до оси рамки).
2. Высота установки, не указанная на плане: выключатели — 900 мм от чистого пола (у кровати и другие — H у марки), со стороны дверной ручки (ПУЭ 7.1.51).
3. Какой выключатель какие светильники включает — по номеру группы L: у выключателя (S1 → L1; L2 — клавиши по порядку) и у каждого светильника. Пунктир подсказка к ближайшему светильнику группы в том же помещении (не дальше 3 м), это не трасса кабеля; выключатель за стеной (у двери санузла) и далёкая группа — только номер группы.
4. Группы из нескольких мест (L1 — S1, S2, S3; L3 — S2, S3; L10 — S6, S12; L19 — S15, S16): на крайних местах — проходные клавиши, на промежуточных перекрёстные; механизмы — в ведомости изделий.
5. Светорегулятор — по заднему фронту (для LED-драйверов), совместимость с драйверами проверить до закупки.
6. Розеточные и мокрые линии — через УЗО или дифавтомат с током утечки не более 30 мА (ПУЭ 7.1.79); в санузле выполнить ДСУП (ПУЭ 7.1.87–7.1.88).
7. Кабель — медный, исполнение нг(A)-LS (ГОСТ 31565-2012); скрытая прокладка только горизонтально и вертикально, фактические трассы зафиксировать исполнительной схемой до закрытия отделкой.
8. Расчёт нагрузок, токов КЗ, селективности и сечений — по проекту ЭОМ организации с допуском СРО; лист задаёт состав, расположение и группы.

| | | | | | | |
|---|---|---|---|---|---|---|
| | | | | | Проект: Квартира с кабинетом | М 1:50 |
| | Лист | № док. | Подпись | Дата | | |
| Дизайнер | Кырлан А.С. | | | 04.11.26 | Управление светильниками | Стадия: П; Лист: 69; Листов: 127 |

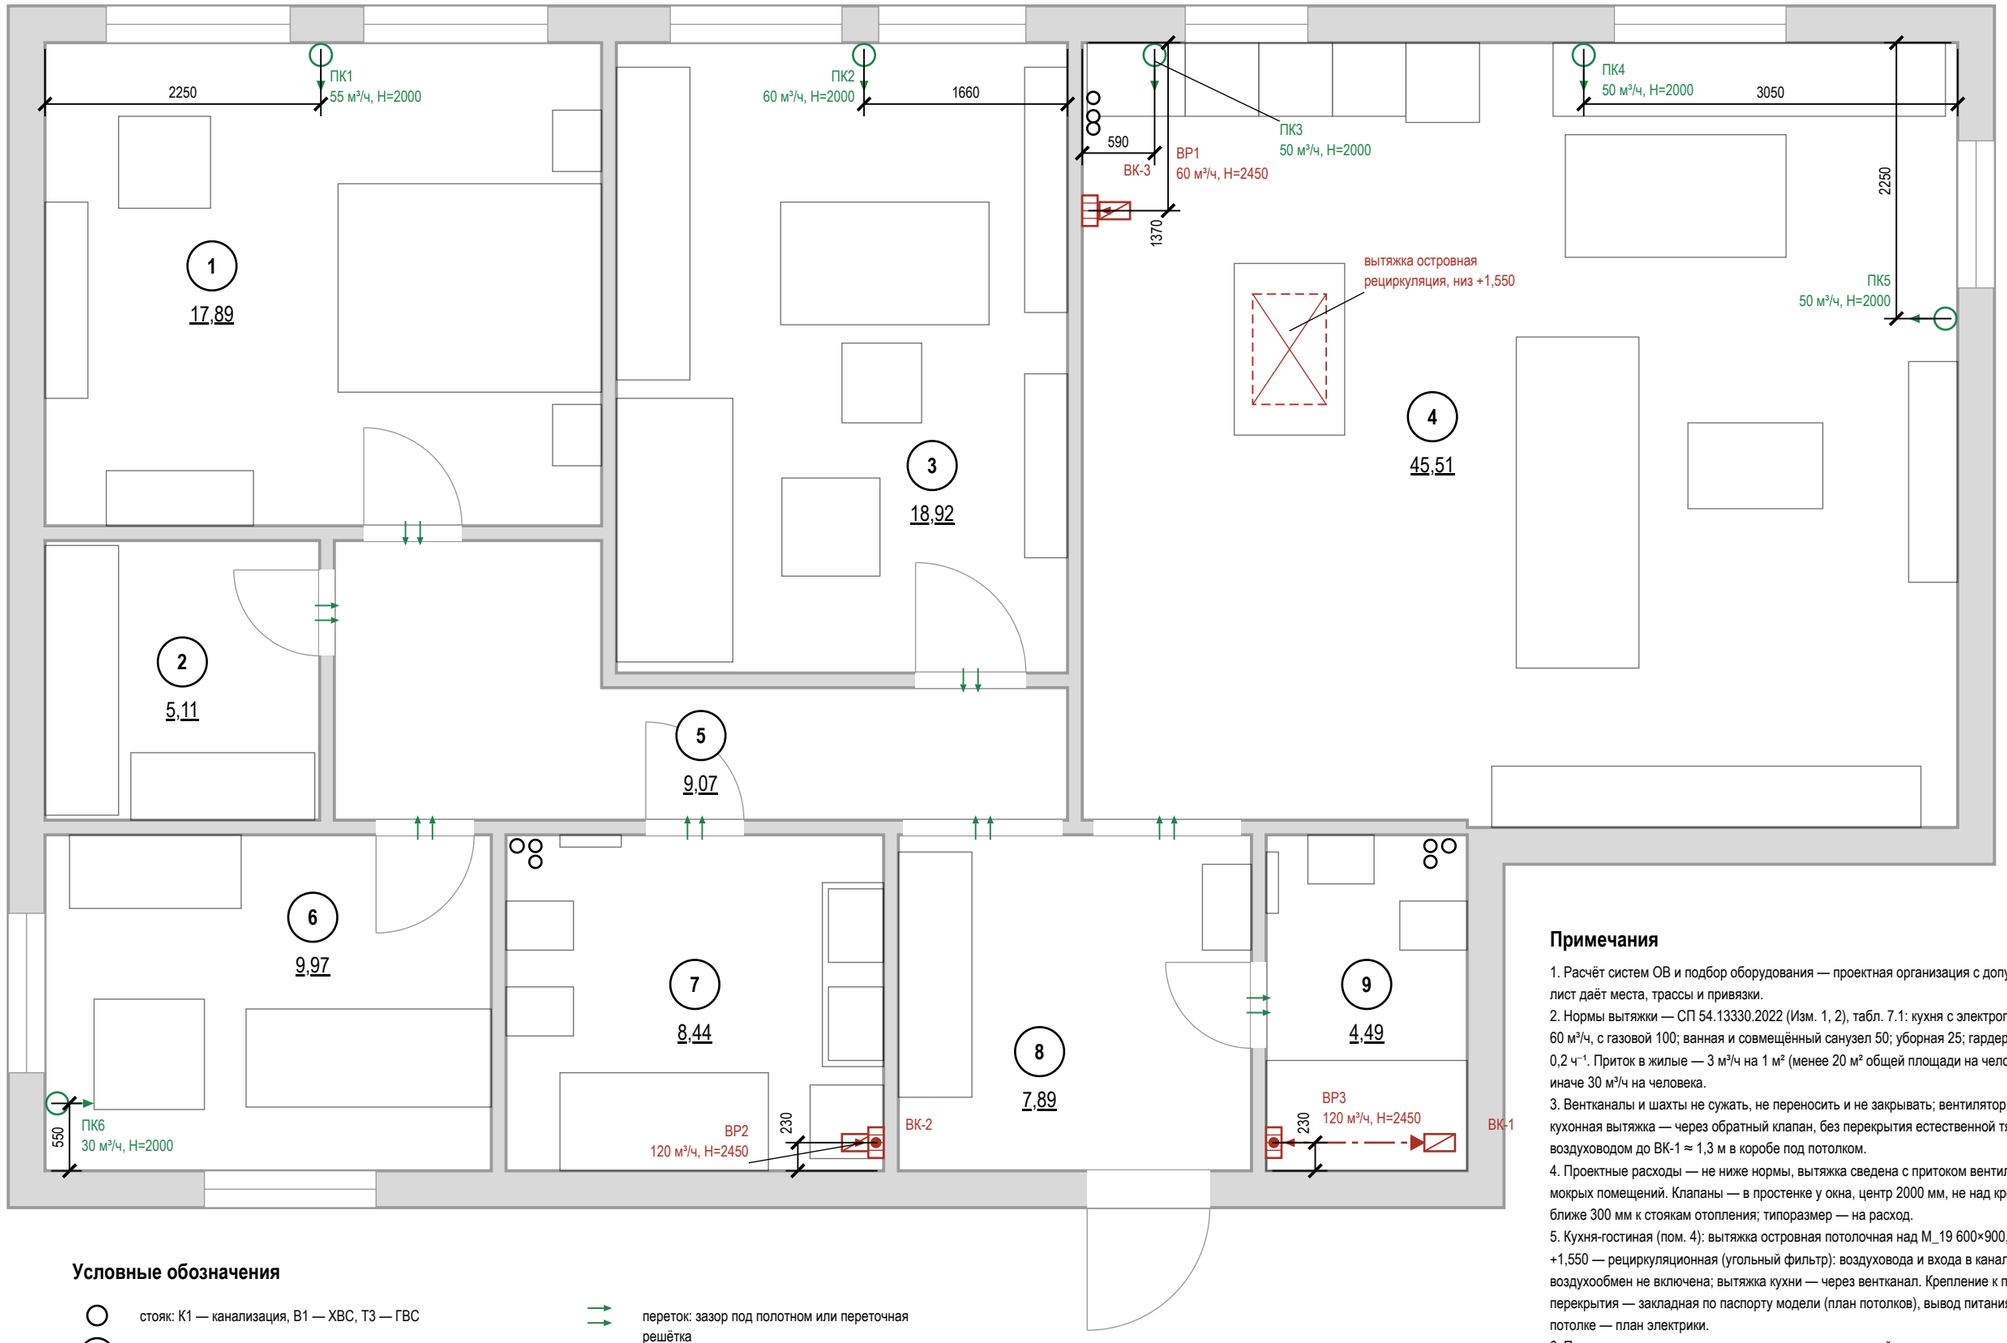


## Условные обозначения


- стояк: К1 — канализация, В1 — ХВС, Т3 — ГВС
- (1) номер помещения, площадь м²
- вытяжная решётка в вентканал: марка, расход м³/ч, Н центра от чистого пола
- вытяжная решётка с бытовым вентилятором и обратным клапаном: марка, расход, Н
- приточный клапан (КИВ) в наружной стене: марка, расход, Н центра
- переток: зазор под полотном или переточная решётка
- кухонная вытяжка над варочной панелью
- вентканал ВК-N в стене или вентблоке
- воздуховод в коробе под потолком (за подшивным потолком) до вентканала
- отдельный вход воздуховода в вентканал, обратный клапан

## Примечания

1. Расчёт систем ОВ и подбор оборудования — проектная организация с допуском СРО; лист даёт места, трассы и привязки.
2. Нормы вытяжки — СП 54.13330.2022 (Изм. 1, 2), табл. 7.1: кухня с электроплитой 60 м³/ч, с газовой 100; ванная и совмещённый санузел 50; уборная 25; гардеробная 0,2 ч⁻¹. Приток в жилые — 3 м³/ч на 1 м² (менее 20 м² общей площади на человека), иначе 30 м³/ч на человека.
3. Вентканалы и шахты не сужать, не переносить и не закрывать; вентилятор и кухонная вытяжка — через обратный клапан, без перекрытия естественной тяги; ВР3 воздуховодом до ВК-1 ≈ 1,3 м в коробе под потолком.
4. Проектные расходы — не ниже нормы, вытяжка сведена с притоком вентиляторами мокрых помещений. Клапаны — в простенке у окна, центр 2000 мм, не над кроватью, не ближе 300 мм к стоякам отопления; типоразмер — на расход.
5. Кухня-гостиная (пом. 4): вытяжка островная потолочная над М_19 600×900, низ +1,550 — рециркуляционная (угольный фильтр): воздуховода и входа в канал нет, в воздухообмен не включена; вытяжка кухни — через вентканал. Крепление к плите перекрытия — закладная по паспорту модели (план потолков), вывод питания на потолке — план электрики.
6. Переток — зазор под полотнами межкомнатных дверей или переточная решётка.
7. Кондиционирование заданием не предусмотрено; при установке трассы фреона и дренажа (не менее 40 мм/м, в К1 через сифон) и питание заложить до черновых работ.
8. Привязки оборудования — по паспортам приобретённых моделей, до черновых работ.

| | | | | | | |
|---|---|---|---|---|---|---|
| | | | | | Проект: Квартира с кабинетом | М 1:50 |
| | Лист | № док. | Подпись | Дата | План вентиляции | Стадия / Лист / Листов |
| Дизайнер | Кырлан А.С. | | | 04.11.26 | | П / 70 / 127 |

выпуск 04.11.2026 № 627e1ac6ce · стр. 70 из 127

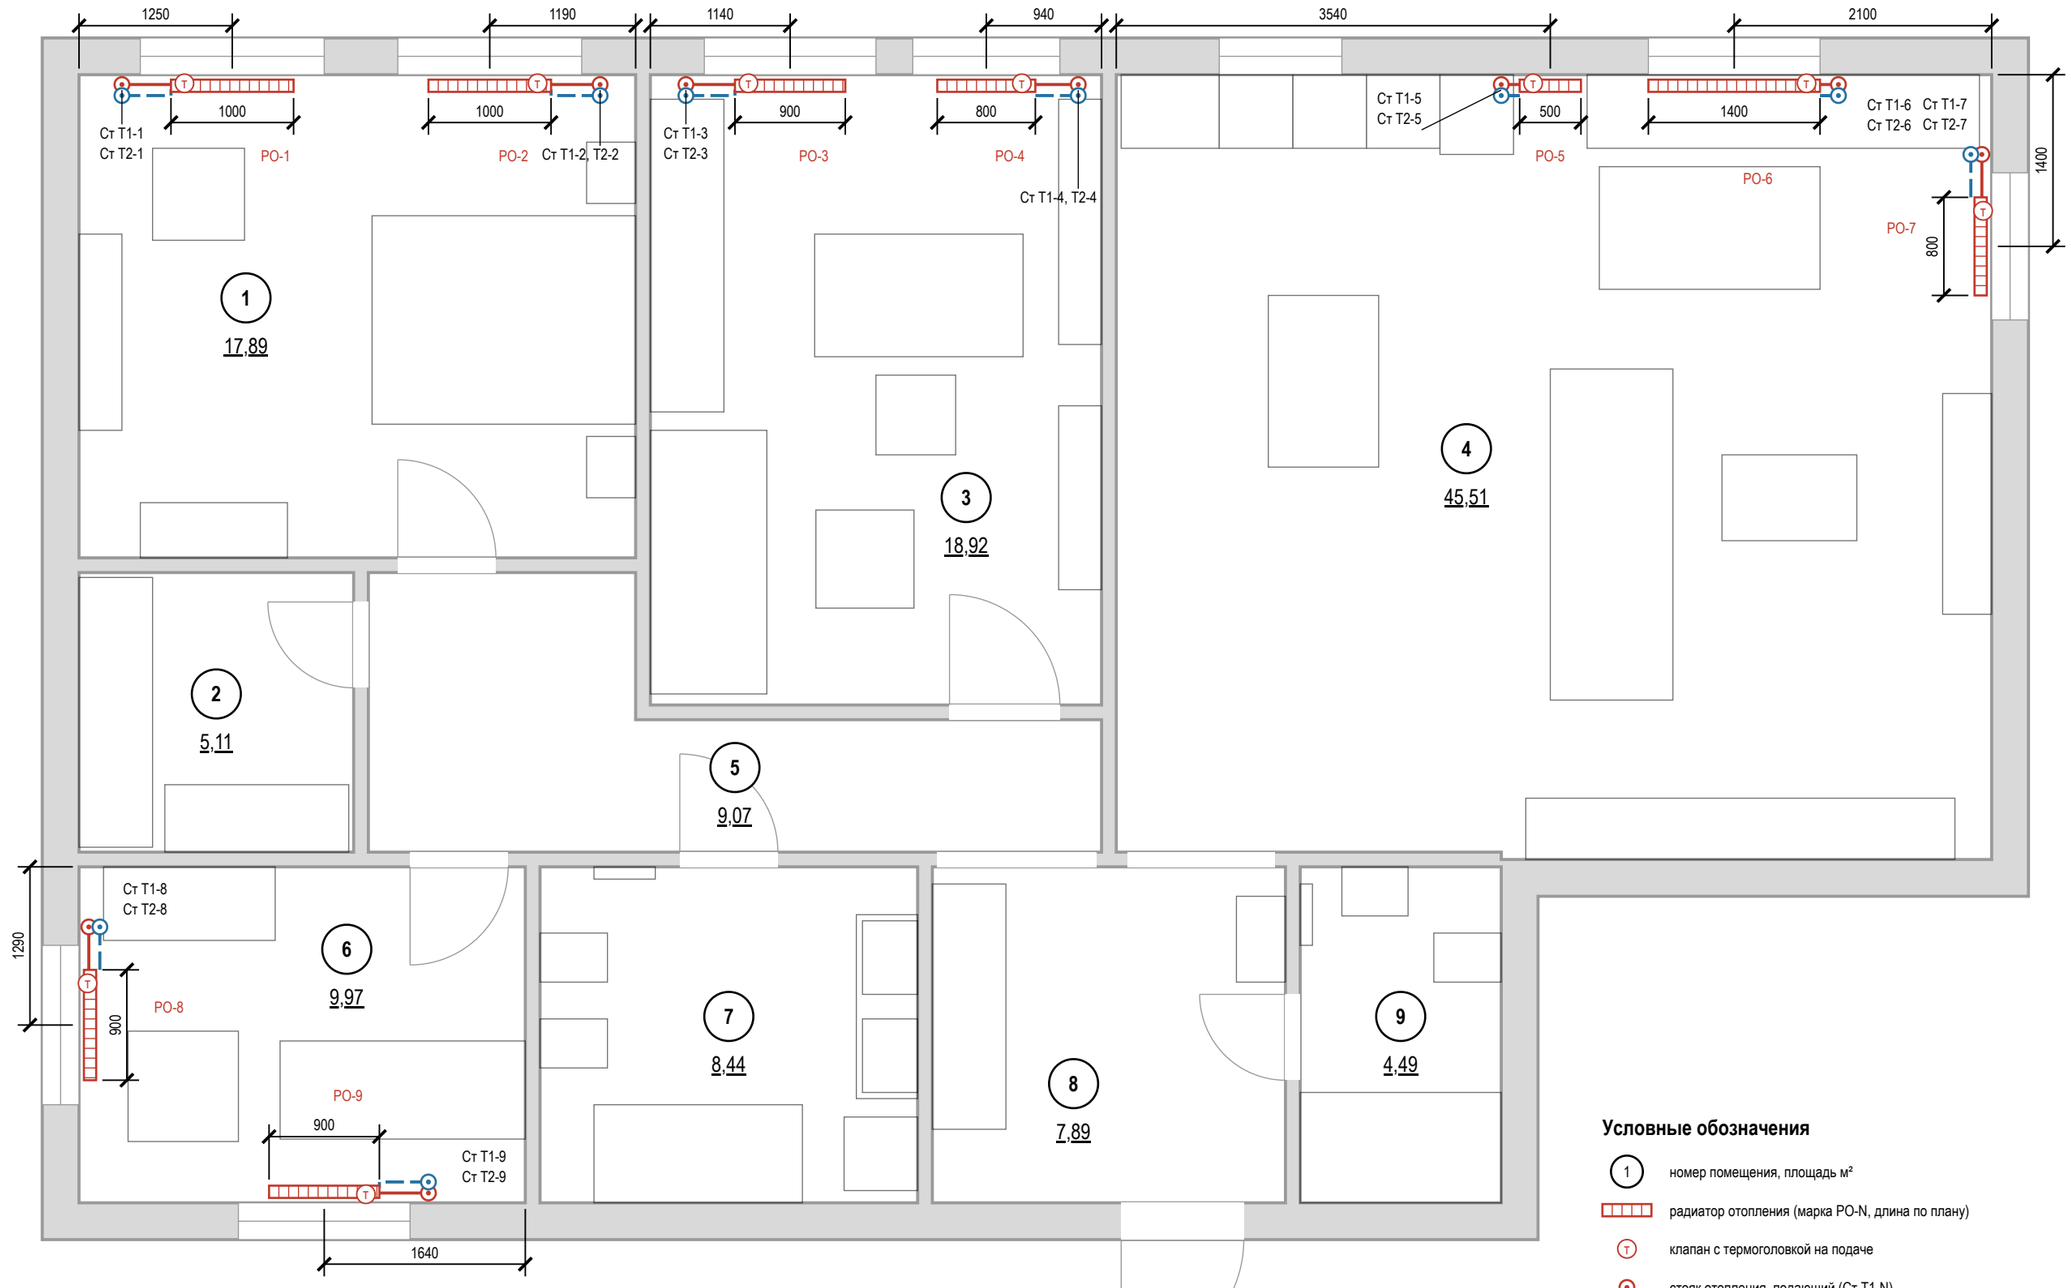


## Условные обозначения

- (1) — номер помещения, площадь м²
- радиатор отопления (марка PO-N, длина по плану)
- (T) — клапан с термоголовкой на подаче
- стояк отопления, подающий (Ст T1-N)
- стояк отопления, обратный (Ст T2-N)
- T1 — отопление, подающий трубопровод
- T2 — отопление, обратный трубопровод

## Примечания


1. Расчёт системы отопления, теплопотерь и подбор приборов — проектная организация с допуском СРО; лист даёт места и привязки.
2. Тип, длина и мощность радиаторов — по теплотехническому расчёту; лист задаёт места, зазоры и подключение.
3. Зазоры радиатора: низ не менее 100 мм от чистого пола, верх не менее 100 мм до подоконника, 30–50 мм от стены до задней панели; центр по оси окна с допуском ±20 мм. Верх до подоконника — 180 мм (PO-6 — 580).
4. Радиаторы не закрывать глухими коробами и мебелью; перенос и замена приборов в многоквартирном доме — переустройство, согласование с управляющей организацией (ЖК РФ ст. 25–26); вынос на лоджию запрещён.
5. Исключение — экран-мебель с решёткой: M_20 (пом. 4), щель 60 мм у стены, решётка в лицевой панели, зазор до прибора 50 мм: теплоотдача прибора за экраном снижается — мощность с учётом экрана по теплотехническому расчёту; сиденье над прибором — съёмное для доступа к крану.
6. Трубы отопления через межквартирные стены не прокладывать (СП 51.13330.2011, п. 9.19); через перекрытия и перегородки — в гильзах.
7. Привязки приборов и подводок — по паспортам приобретённых радиаторов и клапанов, до черновых работ.
8. Привязки — до обмера: Стояки отопления в исходных данных не заданы: показаны у откосов окон и у торцов приборов, подводки — принципиально. До черновых работ — обмер стояков и паспорта приборов; лист перевыпустить по факту.
9. До закрытия отделкой трубопроводы отопления испытать гидростатическим давлением с оформлением акта (СП 73.13330.2016, 7.2–7.3).

| | | | | | |
|---|---|---|---|---|---|
| | | | | | Проект: Квартира с кабинетом — М 1:50 |
| | Лист | № док. | Подпись | Дата | План отопления |
| Дизайнер | Кырлан А.С. | | | 04.11.26 | Стадия: П; Лист: 71; Листов: 127 |




выпуск 04.11.2026 № 627e1ac6ce · стр. 71 из 127

## Отметки по высоте

**±0,000** чистый пол пом. 1–6, 8; отсчёт высот
**−0,015** чистый пол пом. 7, 9, ниже на 15 мм
**−0,064** верх плиты — расчёт, не замер (задание на обмер)
**сущ. пол** снимается до плиты; не замерен (задание на обмер)

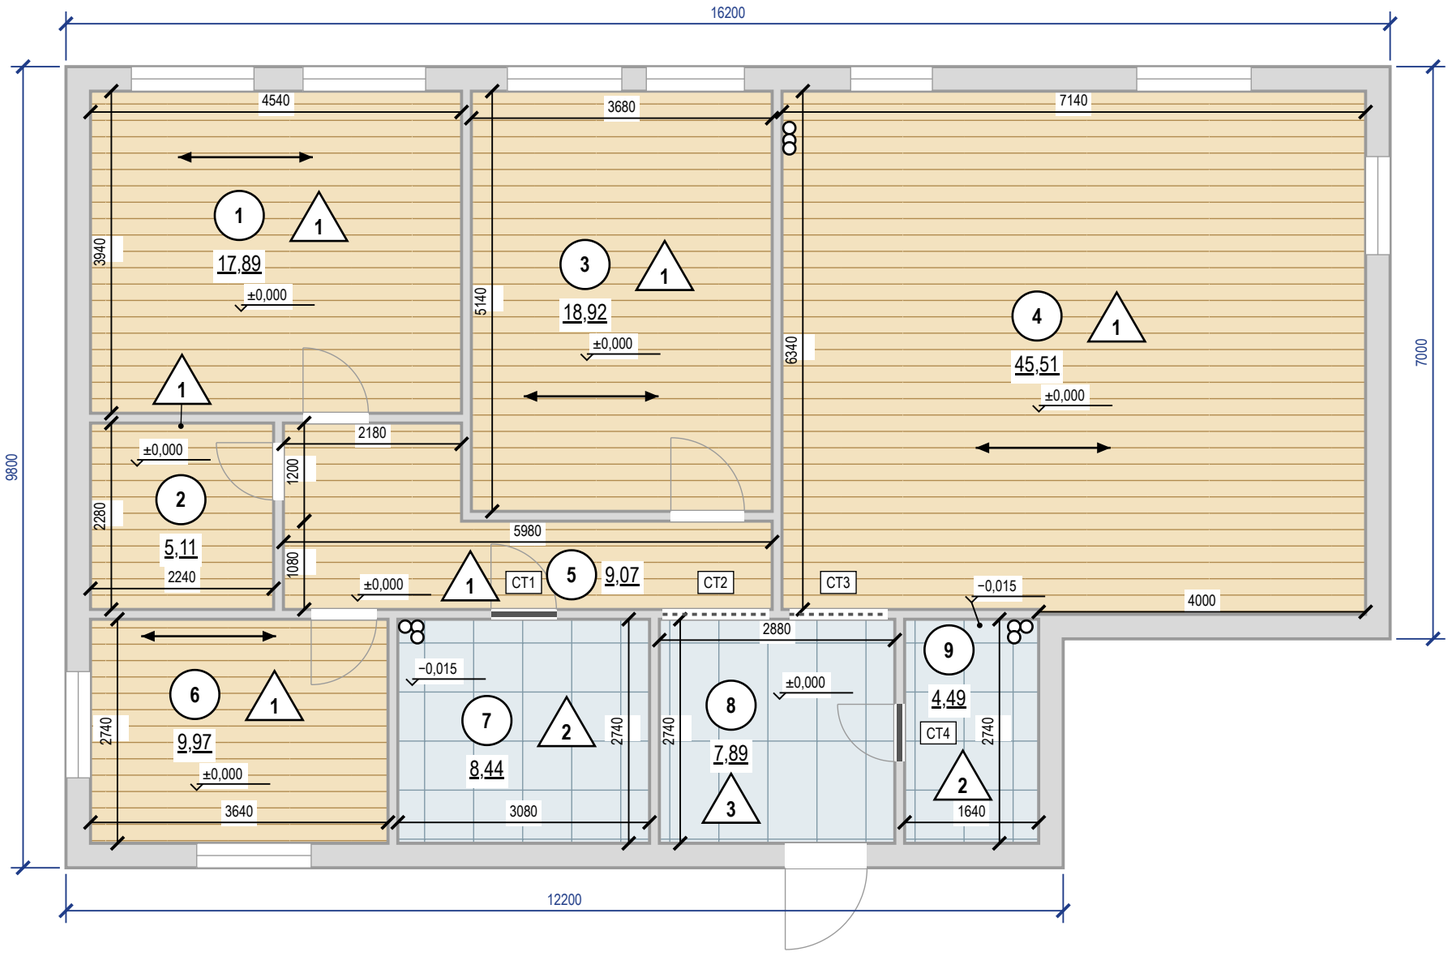


## Экспликация полов
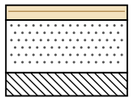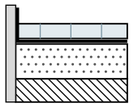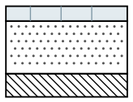
| Номер помещения | Тип пола | Схема пола | Данные элементов пола (наименование, толщина, основание), мм | Площадь, м² |
|---|---|---|---|---|
| 1, 2, 3, 4, 5, 6 | 1 |  | Инженерная доска на клею — 14<br>Стяжка ЦПС М200 — 50<br>Плита перекрытия<br>Всего 64 мм; ЧП ±0,000, верх плиты −0,064 | 106,47 |
| 7, 9 | 2 |  | Керамогранит на клею C2 TE S1 — 14<br>Гидроизоляция обмазочная, 2 слоя, с заведением на стены 200 мм — 2<br>Стяжка ЦПС М200 — 33<br>Плита перекрытия<br>Всего 49 мм; ЧП −0,015, верх плиты −0,064 | 12,93 |
| 8 | 3 |  | Керамогранит на клею C2 TE S1 — 14<br>Стяжка ЦПС М200 — 50<br>Плита перекрытия<br>Всего 64 мм; ЧП ±0,000, верх плиты −0,064 | 7,89 |
| | | | **Итого** | **127,29** |

## Раскладка покрытий

| Пом. | Укладка | Старт (оси от чистовых стен), мм | Отступ 1-го ряда / крайние плитки, мм |
|---|---|---|---|
| 1 | вдоль стен А/В, прямая | от стены А, 1-й ряд вдоль неё | зазор от стены не задан |
| 2 | вдоль стен А/В, прямая | от стены А, 1-й ряд вдоль неё | зазор от стены не задан |
| 3 | вдоль стен А/В, прямая | от стены А, 1-й ряд вдоль неё | зазор от стены не задан |
| 4 | вдоль стен А/В, прямая | от стены А, 1-й ряд вдоль неё | зазор от стены не задан |
| 5 | вдоль стен А/В, прямая | от стены А, 1-й ряд вдоль неё | зазор от стены не задан |
| 6 | вдоль стен А/В, прямая | от стены В, 1-й ряд вдоль неё | зазор от стены не задан |
| 7 | прямая, сетка 600×600, шов 2 | ось X 1516 от Г; ось Y 1346 от А | X 311 / 311; Y 442 / 442 |
| 8 | плитка | раскладка плиточника не задана | |
| 9 | прямая, сетка 600×600, шов 2 | ось X 796 от Г; ось Y 1346 от А | X 494 / 494; Y 442 / 442 |

## Спецификация плинтусов

| Наименование | Помещения | Длина, м (с запасом) |
|---|---|---|
| Плинтус МДФ под покраску 80×16, крепление к стене, окраска в цвет Farrow & Ball No. 15 | 1, 3, 4, 5, 8 | 85 |
| Плинтус МДФ под покраску 80×16, крепление к стене, окраска в цвет Tikkurila V503 | 2 | 10 |
| SX165, h = 69 мм, крепление к стене, окраска в цвет Farrow & Ball No. 15 | 6 | 14 |


## Примечания

1. За отметку ±0,000 принят чистый пол, не существующий (блок отметок). Площади — по чистым размерам помещений, м²; размеры — в мм.
2. Стык разнотипных покрытий — по оси дверного полотна (под полотном в закрытом положении); решение стыка — по ведомости стыков.
3. Пол санузлов ниже смежных помещений на 15 мм за счёт меньшей толщины стяжки (верх плиты общий — по экспликации полов); гидроизоляция по стяжке с заведением на стены не менее 200 мм (СП 29.13330.2011, п. 7.2), до облицовки — тест проливом и акт скрытых работ.
4. Трубопроводы в конструкции пола не прокладываются: пирог пола 49–64 мм не вмещает выпуски канализации с уклоном — выпуски К1 ведутся по стенам над чистым полом в коробах (лист 43).
5. Звукоизоляционный слой под стяжкой проектом не предусмотрен (стяжка по плите): приведённый уровень ударного шума перекрытия с полом Lnw не более 60 дБ (СП 51.13330.2011, табл. 2) подтвердить по данным дома; при превышении — плавающая стяжка по звукоизоляции с демпферной лентой по контуру и у стояков, пирог пересчитать.
6. Штучные покрытия (инженерная доска): направление — по стрелке; влажность основания по СМ не более 2,0 % (по ТУ изготовителя).
7. Ровность основания — просвет под 2-метровой рейкой не более 2 мм: пом. 1, 2, 3, 4, 5, 6 (инженерная доска), пом. 7, 8, 9 (керамогранит); проверить до укладки покрытия (СП 71.13330.2017, табл. 8.5).
8. Сетка на плитке — условная, в размер формата; точка старта и раскладка — по листу раскладки плитки.
9. Узор покрытия (заливка-код типа пола) прерывается под надписями — площадями помещений и отметками чистого пола.
10. Пироги полов — по экспликации полов: слои сверху вниз, толщины в мм; гидроизоляция мокрых зон — в пироге и в ведомости отделки; схема пола — без масштаба.


| | | | | | |
|---|---|---|---|---|---|
| | | | | | Проект: Квартира с кабинетом — **М 1:75** |
| | Лист | № док. | Подпись | Дата | |
| Дизайнер | Кырлан А.С. | | | 04.11.26 | План покрытий пола |
| | | | | | Стадия: П; Лист: 72; Листов: 127 |

выпуск 04.11.2026 № 627e1ac6ce · стр. 72 из 127

**Фрагмент 1. Ванная (пом. 7). Пол 600×600, шов 2 мм, М 1:40**

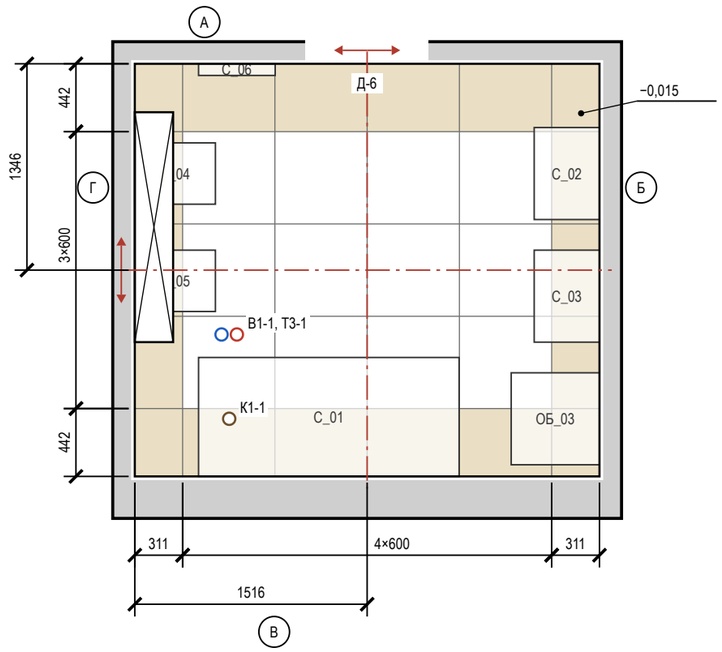


**Фрагмент 2. Санузел гостевой (пом. 9). Пол 600×600, шов 2 мм, М 1:40**

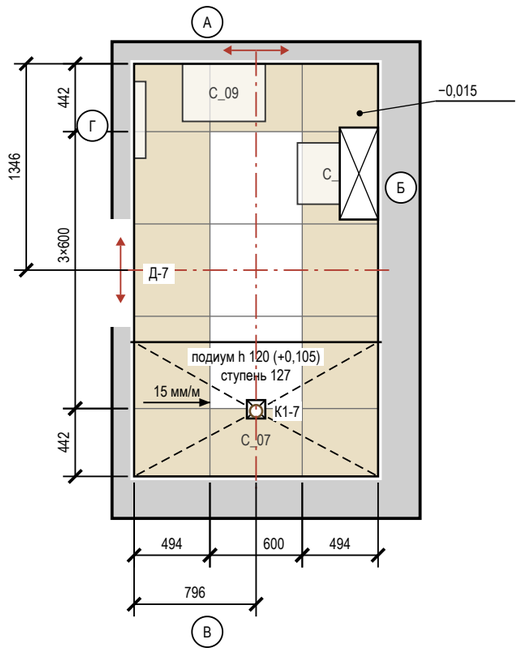


## Условные обозначения

- плитка целая; тонкая линия — шов
- плитка с подрезкой (размер — на цепочке)
- ось старта; стрелки — направление укладки
- сантехприбор: габарит, высота по практике
- короб инсталляции: плитка пола — до короба
- трап / лоток в полу
- направление уклона К1 / пола: Ø, мм на 1 м
- край подиума; штрих — конверт к трапу
- вывод В1 (код — в ведомости привязок)
- вывод Т3 (код — в ведомости привязок)
- вывод К1 (код — в ведомости привязок)
- отметка чистого пола на полке выноски, м
- А — обозначение стены А–Г (как на развёртках)

## Ведомость плитки

| Помещение, поверхность | Плитка, код | Формат | Шов | S, м² | Целых | Подр. | С запасом |
|---|---|---|---|---|---|---|---|
| Ванная, пол | аналог: керамогранит под травертин | 600×600 | 2 | 8,44 | 12 | 18 | 33 |
| Ванная, стены А–Г | A8UZ | 600×1200 | 2 | 26,96 | 9 | 55 | 72 |
| Ванная, короб инсталляции | A8UZ | 600×1200 | 2 | 2,77 | 1 | 7 | 9 |
| Санузел гостевой, пол | аналог: керамогранит под травертин | 600×600 | 2 | 4,49 | 3 | 13 | 18 |
| Санузел гостевой, стены А–Г | A8UZ | 600×1200 | 2 | 20,72 | 4 | 42 | 52 |
| Санузел гостевой, короб инсталляции | A8UZ | 600×1200 | 2 | 1,47 | 1 | 3 | 5 |
| Прихожая, пол | A8UZ | 600×1200 | 2 | 7,89 | 3 | 12 | 17 |
| Кухня-гостиная, фартук (ст. А) | аналог: керамогранит под травертин, матовый | 1200×600 | 2 | 0,70 | 0 | 2 | 3 |
| Итого 600×600 | | | | 12,93 | 15 | 31 | 51 |
| **Итого 600×1200** | | | | **60,51** | **18** | **121** | **158** |

## Ведомость материалов


| Материал | Класс, код | Норма расхода | Кол-во |
|---|---|---|---|
| Затирка | CG2WA Mapei Ultracolor Plus 132 | (a+b)/ab·шов·t·1,6 | 5,3 кг |
| Затирка | CG2WA | (a+b)/ab·шов·t·1,6 | 0,7 кг |
| Клей | C2 TE S1 Ceresit CM 17 | 1,5 кг/м²·мм, слой 5 | 521 кг (21 меш.) |
| Клей | C2 TE S1 | 1,5 кг/м²·мм, слой 5 | 70 кг (3 меш.) |
| Гидроизоляция | обмазочная, 2 слоя: пол, стены по периметру и зоны замачивания | по ТУ | 33,0 м² |
| Демпф. лента | по периметру пола из плитки | | 28,0 м |

## Примечания


1. Раскладка от чистовых размеров: стены санузлов теряют 10 + 5 + 9 = 24 мм на сторону (штукатурка, клей, плитка); подрезки — чистые, без шва.
2. Старт — от центра помещения (штрихпунктир, стрелки — направление укладки); размер старта — от чистовых стен Г и А.
3. Раскладка пола «Прихожая» и фартука «Кухня-гостиная» — на листе «Раскладка плитки. Прихожая. Фартук кухни».
4. Калибр партии не задан — до укладки замерить (рабочий размер W, ГОСТ 13996-2019) и пересчитать подрезки.
5. Количество: целые по раскладке + по одной на подрезку, запас 10 %; один артикул — одна партия и тон. Исключены поддон, короб, проёмы и места за коробом; S — по чистым граням: стены нетто = зона облицовки по ведомости отделки − место за коробом инсталляции 2,52 м² (плитку за коробом не кладут), короб — отдельной строкой.
6. Клей C2 TE S1 Ceresit CM 17; C2 TE S1 (ГОСТ Р 56387-2018), затирка CG2WA Mapei Ultracolor Plus 132; CG2WA; расход — по ТУ выбранной марки.
7. Гидроизоляция: пол и стены 200 мм от ЧП; над ванной — до 2000 и 300 мм за борт (пом. 7), у душа — на всю высоту стен душевой зоны и 500 мм за край душевой зоны (пом. 9) (см. развёртки); акт скрытых работ, пролив 24 ч.
8. Подиум душа С_07 (пом. 9): h 120 у трапа, решётка +0,105; верх — плиткой пола той же раскладки, уклон 15 мм/м к трапу, подрезка по линиям конверта; ступень по краю 127, грань 1592 × 127 = 0,20 м² (+1 шт. в подрезках), угол профилем; гидроизоляция 2 сл. — по плите под подиумом, по верху и грани (узел 1 ВК); предложение, до согласования не выполнять.
9. Швы пола совмещены со швами стены А; по периметру — демпферная лента.
10. Отметка чистого пола −0,015, порог 15 мм; стык с соседним покрытием — по оси полотна двери.

| | | | | | | |
|---|---|---|---|---|---|---|
| | | | | | Проект: Квартира с кабинетом | **М 1:40** |
| | Лист | № док. | Подпись | Дата | | |
| Дизайнер | Кырлан А.С. | | | 04.11.26 | Раскладка плитки. Планы полов | Стадия: П; Лист: 73; Листов: 127 |

**Фрагмент 1. Прихожая (пом. 8). Пол 600×1200, шов 2 мм, М 1:20**

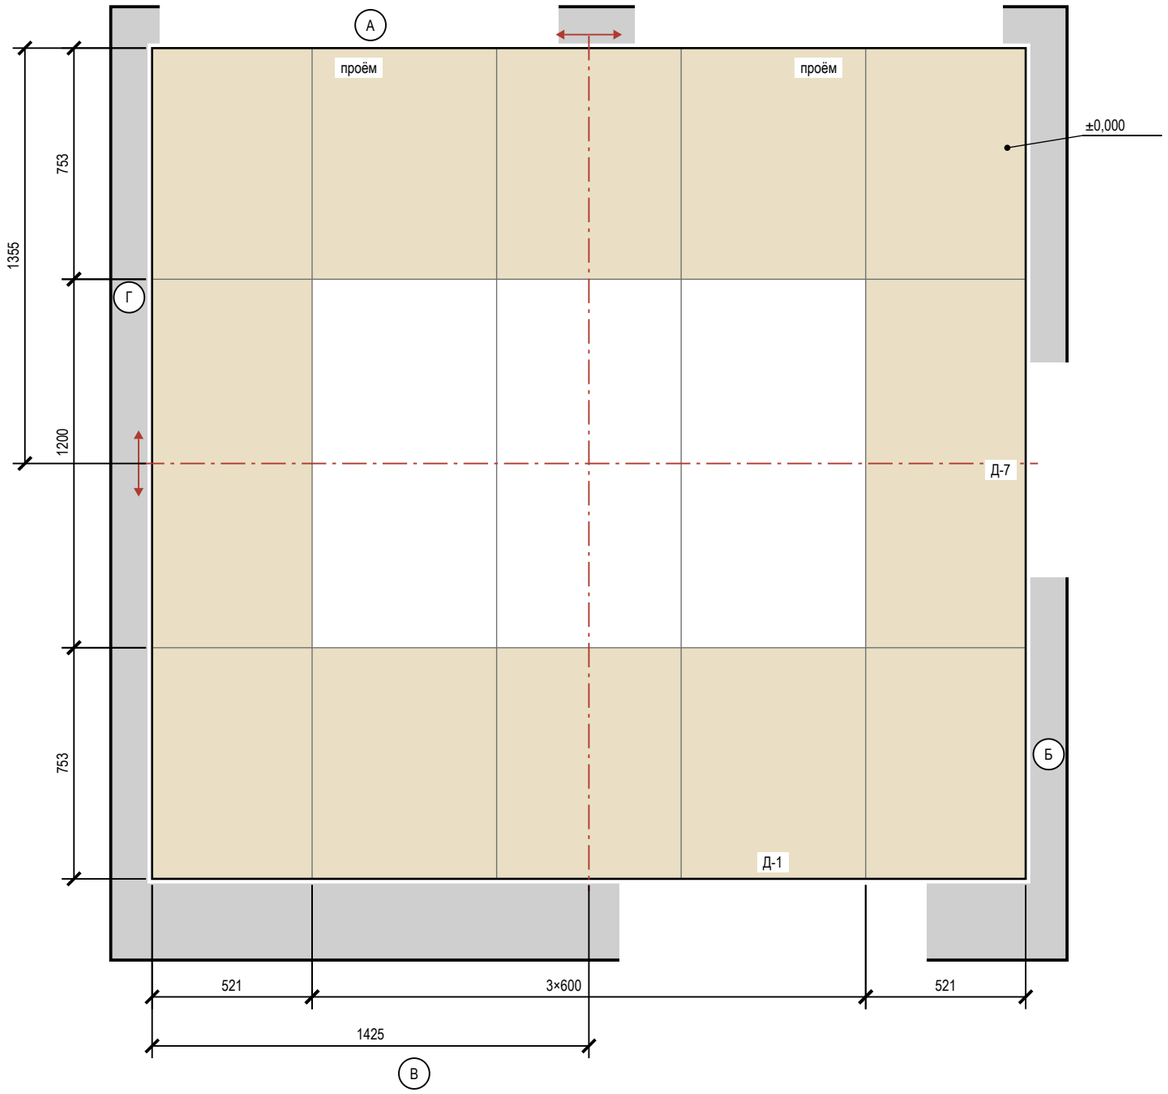


**Фрагмент 2. Кухня-гостиная (пом. 4), фартук, стена А. 1200×600, шов 2 мм, М 1:20**

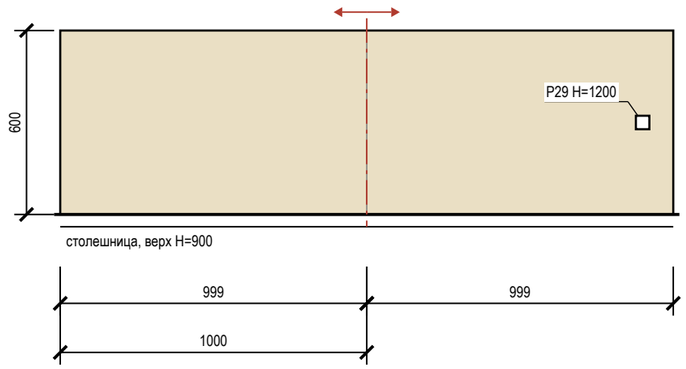


## Условные обозначения

- плитка целая; тонкая линия — шов
- плитка с подрезкой (размер — на цепочке)
- ось старта; стрелки — направление укладки
- электроточка: марка и H — по листам ЭОМ
- столешница (верх)
- навесной шкаф над фартуком
- отметка чистого пола на полке выноски, м
- А — обозначение стены А–Г (как на развёртках)

## Подсчёт плитки


| Поверхность | Формат | S, м² | Целых | Подр. | С запасом |
|---|---|---|---|---|---|
| Прихожая, пол | 600×1200 | 7,89 | 3 | 12 | 17 |
| Кухня-гостиная, фартук (ст. А) | 1200×600 | 0,70 | 0 | 2 | 3 |

## Примечания

1. Прихожая: керамогранит 600×1200, длинная сторона — вдоль стен Б и Г, шов 2 мм, прямая раскладка от центра. Стены окрашены: раскладка от чистового контура минус штукатурка и шпаклёвка 15 мм на сторону (принято); подрезки 521 / 753 мм, срез — под плинтус.
2. Прихожая: деформационный зазор по периметру 8–10 мм под плинтусом; в проёмах — стык с соседним покрытием по оси полотна двери. Клей C2 TE S1, затирка CG2WA.
3. Фартук, Кухня-гостиная: 1200×600 горизонтально, шов 2 мм; зоны 2000 мм — 900…1500 (от столешницы до низа навесного шкафа, без шкафа — 600 мм). Старт от центра участка, подрезки 999 мм. Площадь 0,70 м² — как в ведомости отделки.
4. Фартук — после монтажа столешницы, низ на 2–3 мм выше неё, шов со столешницей — санитарный герметик; навесные шкафы — после фартука. Торцы у пенала и стены — профиль или запил 45°.
5. Клей, затирка и итог по форматам — в ведомостях листа «Раскладка плитки. Планы полов».

| | | | | | | |
|---|---|---|---|---|---|---|
| | | | | | Проект: Квартира с кабинетом | М 1:20 |
| | Лист | № док. | Подпись | Дата | | |
| Дизайнер | Кырлан А.С. | | | 04.11.26 | Раскладка плитки. Прихожая. Фартук кухни | Стадия: П; Лист: 74; Листов: 127 |


## Развёртка стены А

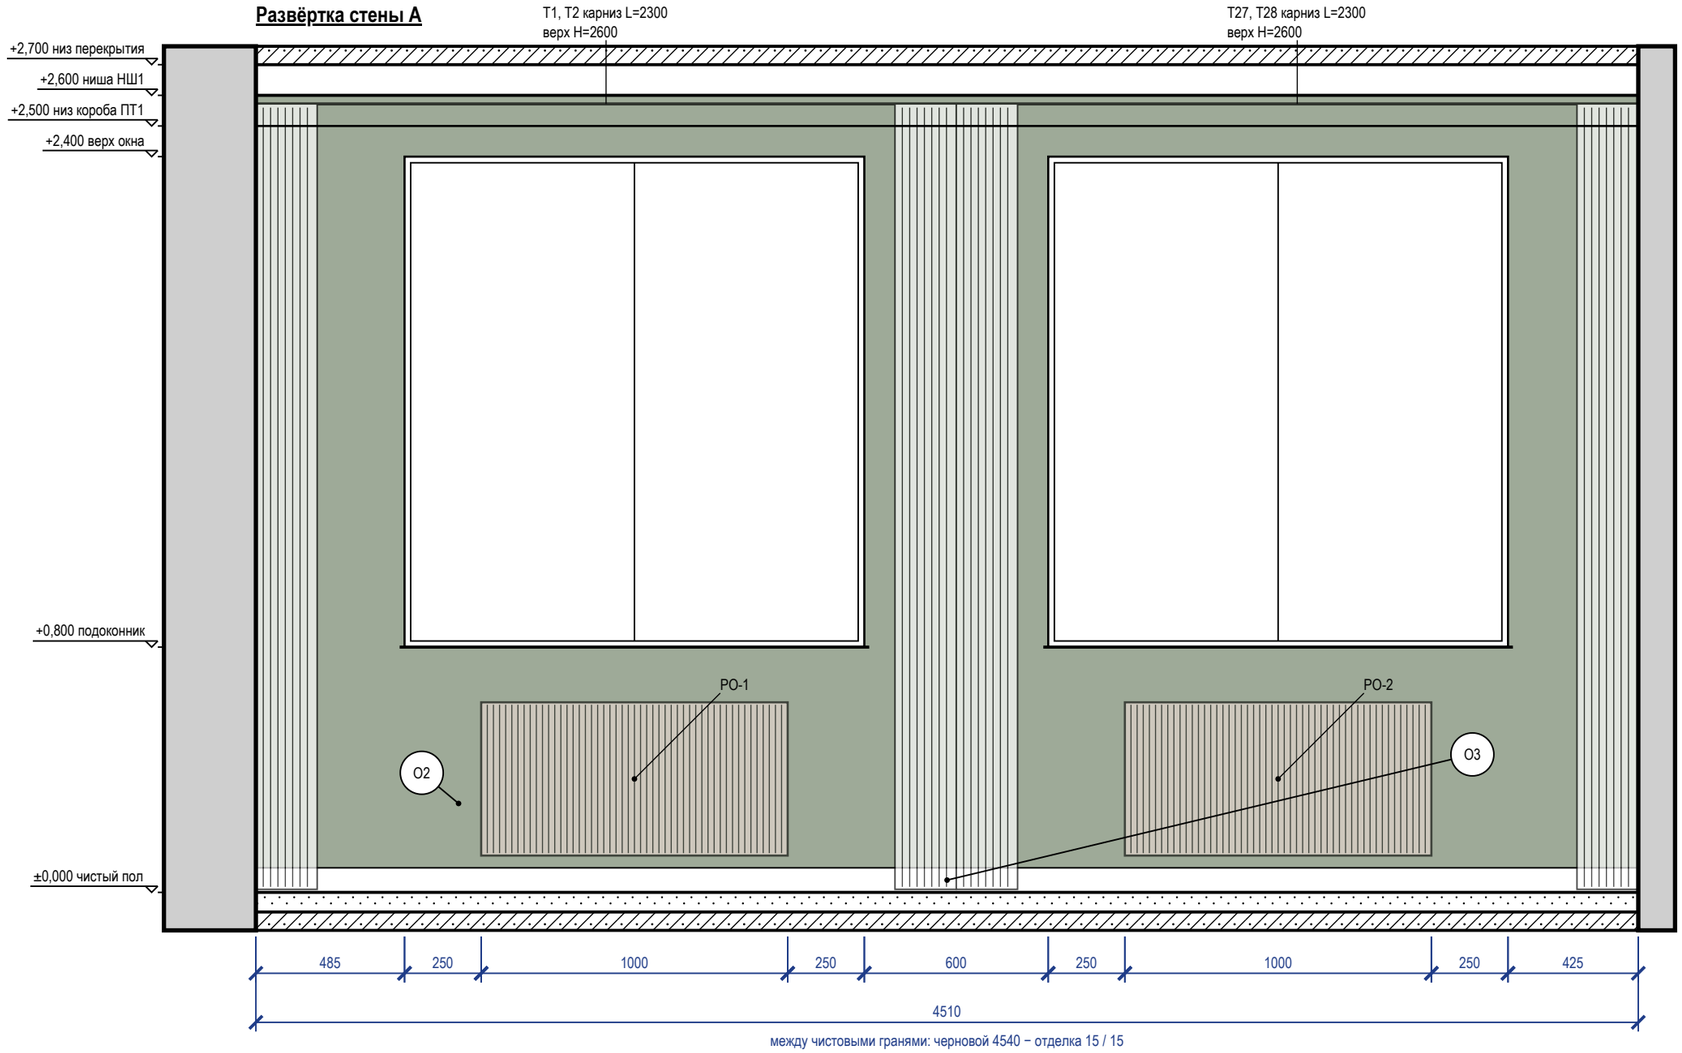


Визуализация этой стены — лист 4



### Схема развёрток (М 1:100)

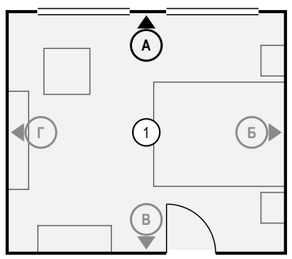


### Ведомость отделки (на листе)


| Марка | Поверхность | Материал, изделие | Цвет, код | Кол. |
|---|---|---|---|---|
| О2 | акцентная стена | окраска, Farrow & Ball Modern Emulsion, матовая, подготовка Q3 | Farrow & Ball No. 34 «Calke Green традиционный шалфей» | 6,9 м² |
| О3 | плинтус | плинтус МДФ, h 80 мм, аналог: плинтус МДФ под покраску 80×16 | Farrow & Ball No. 15 «Bone — мягкий каменно-серый с зеленцой» | 4,5 м |
| О4 | потолок | окраска, Tikkurila Anti-Reflex 2, глубокоматовая, подготовка Q3 | Tikkurila V503 «Winter» | 17,9 м² |

### Примечания


1. Размеры — в мм от чистовых поверхностей стен; условные обозначения и общие указания — лист 27.
2. Карнизы (шины) — по ведомости текстиля декоратора: длина L и верх H на развёртке — те же числа, что в ведомости; крепление — до окраски потолка.
3. Потолок — у каждой стены свой, по плану потолков (НШ1, ПТ1); ступени — зоной, кромка короба перед нишей — тонкой линией; в поле потолка: ПТ2 +2,600.
4. Карниз T1, T2: по ведомости текстиля шина L=2300 мм, а от её начала до чистового угла стены — 2285 мм: шина не встаёт, длину согласовать с декоратором до заказа.
5. Карниз T27, T28: по ведомости текстиля шина L=2300 мм, а от её начала до чистового угла стены — 2225 мм: шина не встаёт, длину согласовать с декоратором до заказа.

| | | | | | | |
|---|---|---|---|---|---|---|
| | | | | | Проект: Квартира с кабинетом | М 1:20 |
| | Лист | № док. | Подпись | Дата | | |
| Дизайнер | Кырлан А.С. | | | 04.11.26 | Развёртка стены А. Спальня (пом. 1) | Стадия: П; Лист: 75; Листов: 127 |

## Развёртка стены Б

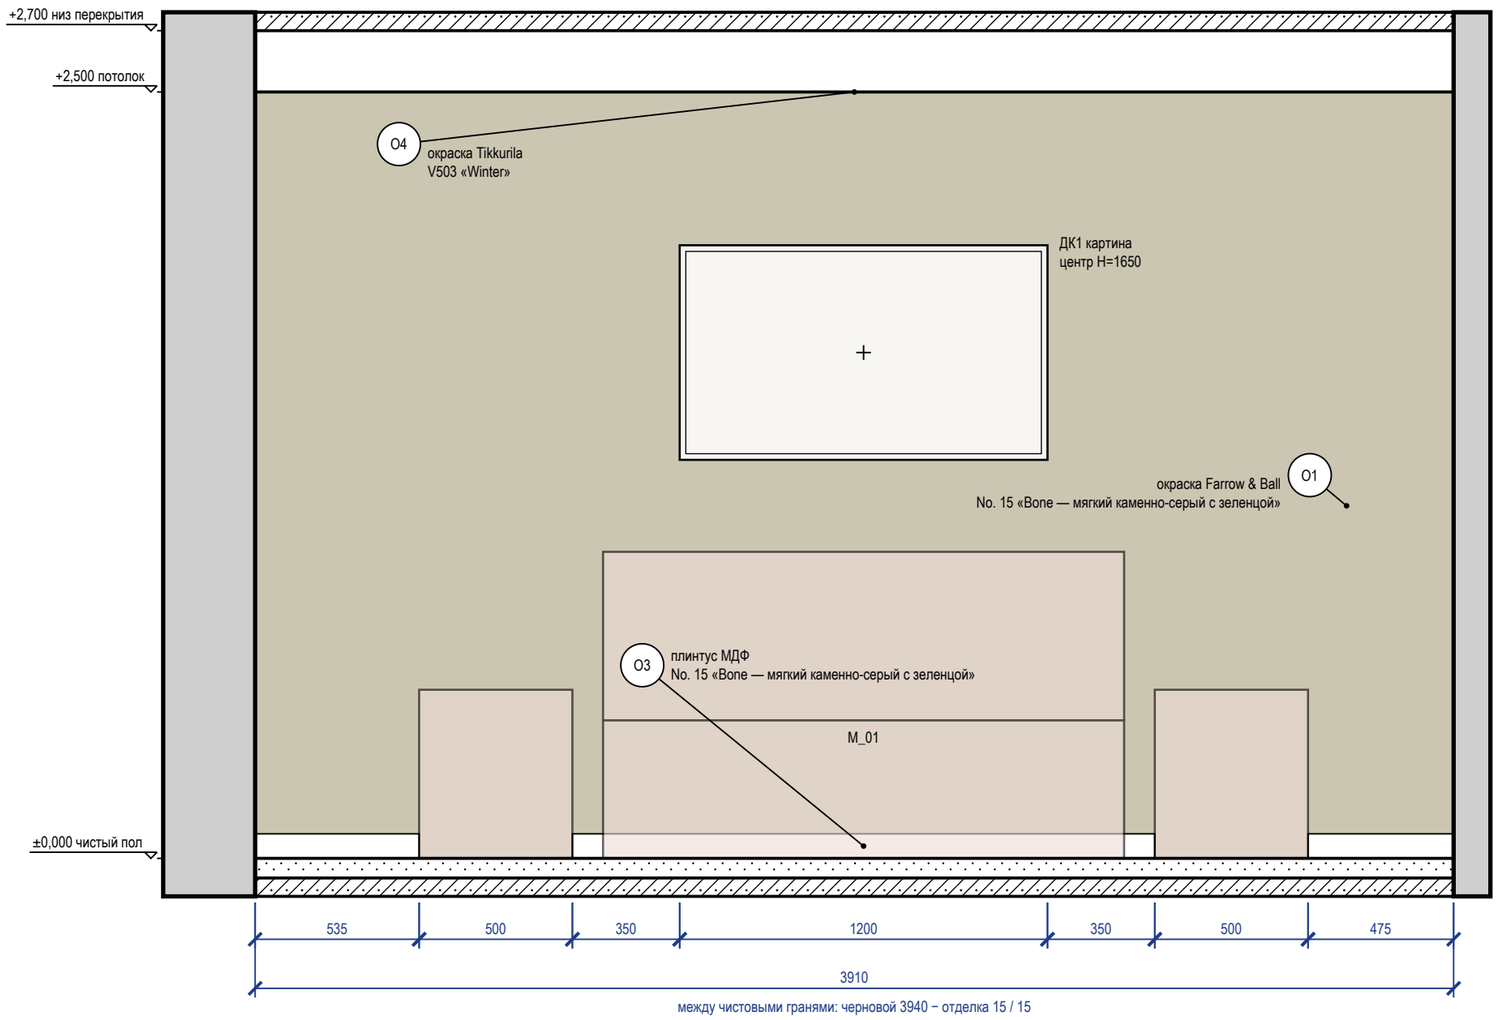


### Схема развёрток (М 1:100)

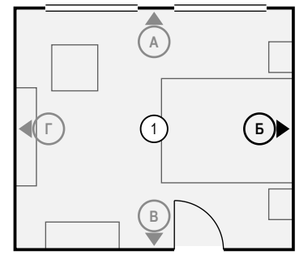


### Ведомость отделки (на листе)

| Марка | Поверхность | Материал, изделие | Цвет, код | Кол. |
|---|---|---|---|---|
| О1 | стены | окраска, Farrow & Ball Modern Emulsion, матовая, подготовка Q3 | Farrow & Ball No. 15 «Bone — мягкий каменно-серый с зеленцой» | 9,8 м² |
| О3 | плинтус | плинтус МДФ, h 80 мм, аналог: плинтус МДФ под покраску 80×16 | Farrow & Ball No. 15 «Bone — мягкий каменно-серый с зеленцой» | 2,9 м |
| О4 | потолок | окраска, Tikkurila Anti-Reflex 2, глубокоматовая, подготовка Q3 | Tikkurila V503 «Winter» | 17,9 м² |

Визуализация этой стены — лист 5




### Примечания

1. Размеры — в мм от чистовых поверхностей стен; условные обозначения и общие указания — лист 27.
2. Стена Б показана двумя видами: здесь — архитектурная развёртка (мебель, отделка, проёмы, высоты), электроточки и выводы ВК с привязками и таблицей — на листе 77 («Привязки»).
3. Картины и зеркала крепить к основанию по паспорту изделия (закладные и анкеры — в перечне скрытых работ); крест — ось центра предмета.
4. Потолок — у каждой стены свой, по плану потолков (ПТ1); ступени — зоной, кромка короба перед нишей — тонкой линией; в поле потолка: ПТ2 +2,600.

| | | | | | | |
|---|---|---|---|---|---|---|
| | | | | | Проект: Квартира с кабинетом | М 1:20 |
| | Лист | № док. | Подпись | Дата | | |
| Дизайнер | Кырлан А.С. | | | 04.11.26 | Развёртка стены Б. Спальня (пом. 1) | Стадия: П; Лист: 76; Листов: 127 |

## Развёртка стены Б: электроточки и выводы

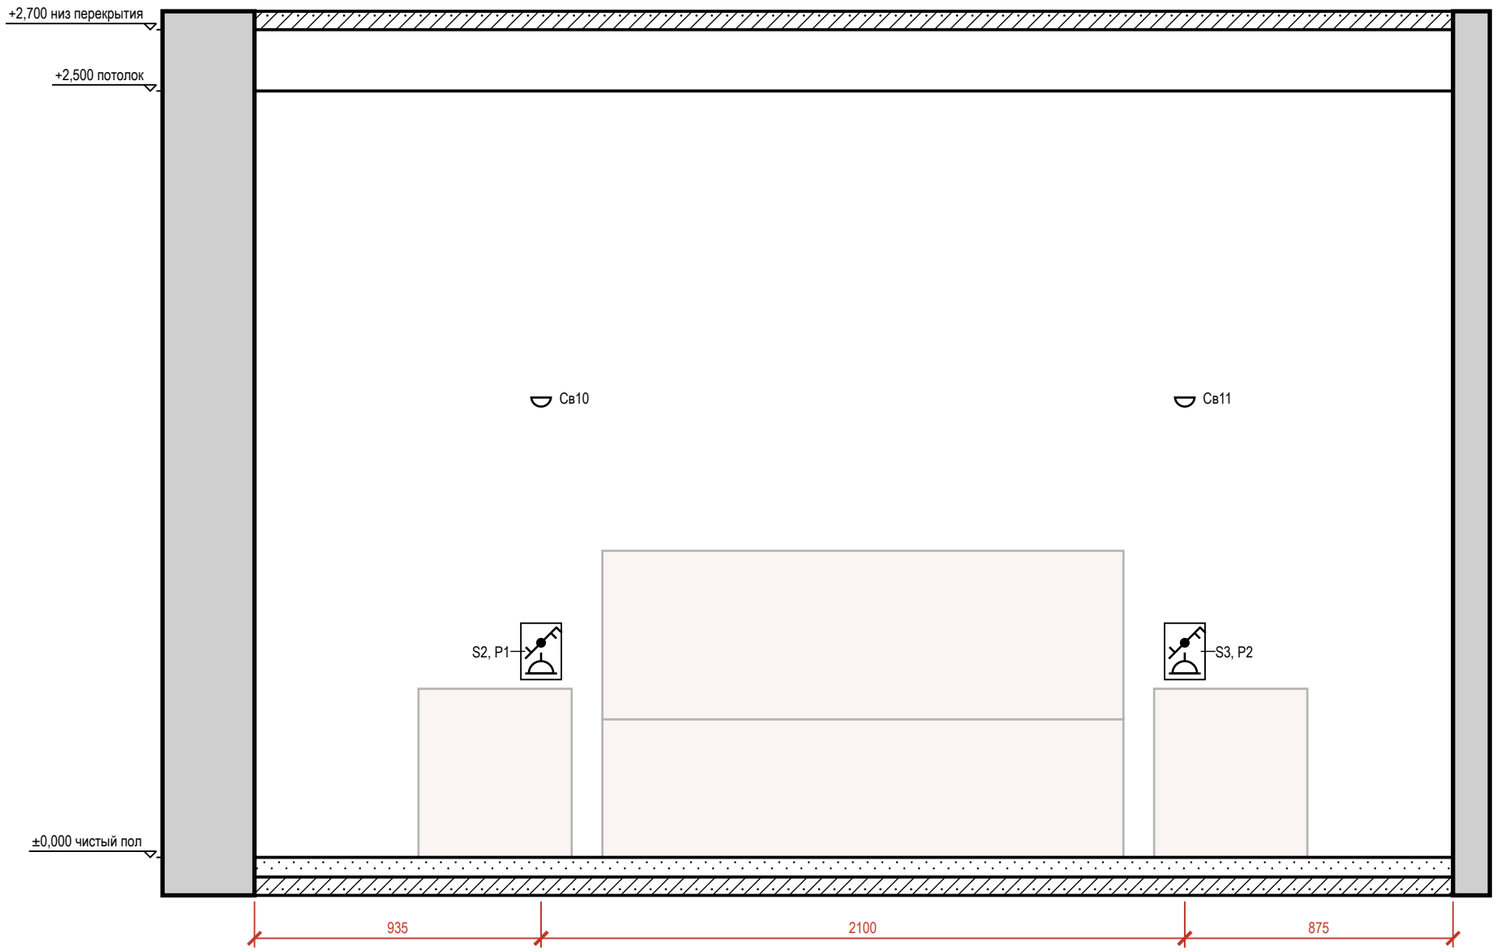



## Таблица привязок электроточек и выводов

| Марка | Назначение | От угла, мм | H от пола, мм | Примечание |
|---|---|---|---|---|
| P1 | розетка: у кровати | 935 | 600 | гр. 4 |
| S2 | выключатель | 935 | 700 | гр. 1 |
| Св10 | светильник настенный | 935 | 1500 | гр. 1 |
| P2 | розетка: у кровати | 3035 | 600 | гр. 4 |
| S3 | выключатель | 3035 | 700 | гр. 1 |
| Св11 | светильник настенный | 3035 | 1500 | гр. 1 |

## Условные обозначения

- розетка с заземляющим контактом; у знака — марка, ×N постов в рамке, гр. — группа щита, H — высота оси, мм
- выключатель одноклавишный
- выключатель двухклавишный (флажков — по числу клавиш)
- выключатель с проходной или перекрёстной клавишей (обратный флажок); тип клавиши — в подписи
- светильник настенный (бра), H — высота оси
- привязки точек и выводов от угла и от пола, мм
- марка развёртки: буква стены, стрелка — взгляд

## Схема развёрток (М 1:50)

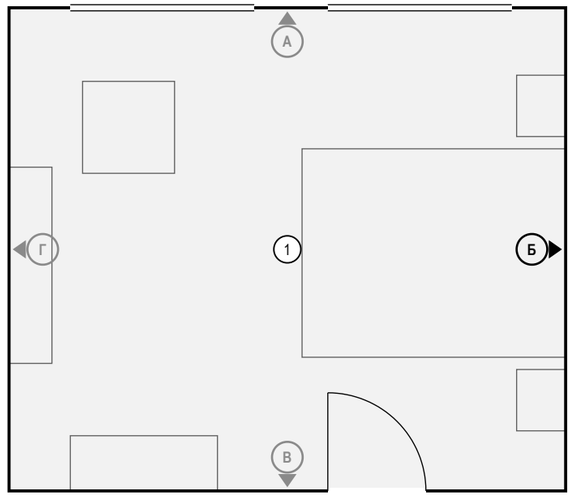



## Примечания


1. Вид «Привязки» стены Б — электроточки и выводы ВК; архитектурная развёртка (мебель, отделка, проёмы, высоты) — на листе 76. Мебель и приборы — подложкой для ориентира; их марки и обозначения мебели, проёмов и стен — там же.
2. Привязки — в мм: по горизонтали от левого чистового угла стены до оси изделия, H — от чистого пола до оси; все точки — в таблице привязок. Красная цепочка — привязки по осям; точки ближе 120 мм одна к другой в цепочку не дробятся — их привязки только в таблице.
3. У знака — марка электроточки (P — розетка, S — выключатель, Св — светильник, ЭВ — вывод кабеля); условные обозначения и общие указания — лист 27.

| | | | | | | |
|---|---|---|---|---|---|---|
| | | | | | Проект: Квартира с кабинетом | М 1:20 |
| | Лист | № док. | Подпись | Дата | | |
| Дизайнер | Кырлан А.С. | | | 04.11.26 | Привязки электроточек, стена Б. Спальня (пом. 1) | Стадия: П; Лист: 77; Листов: 127 |

## Развёртка стены В

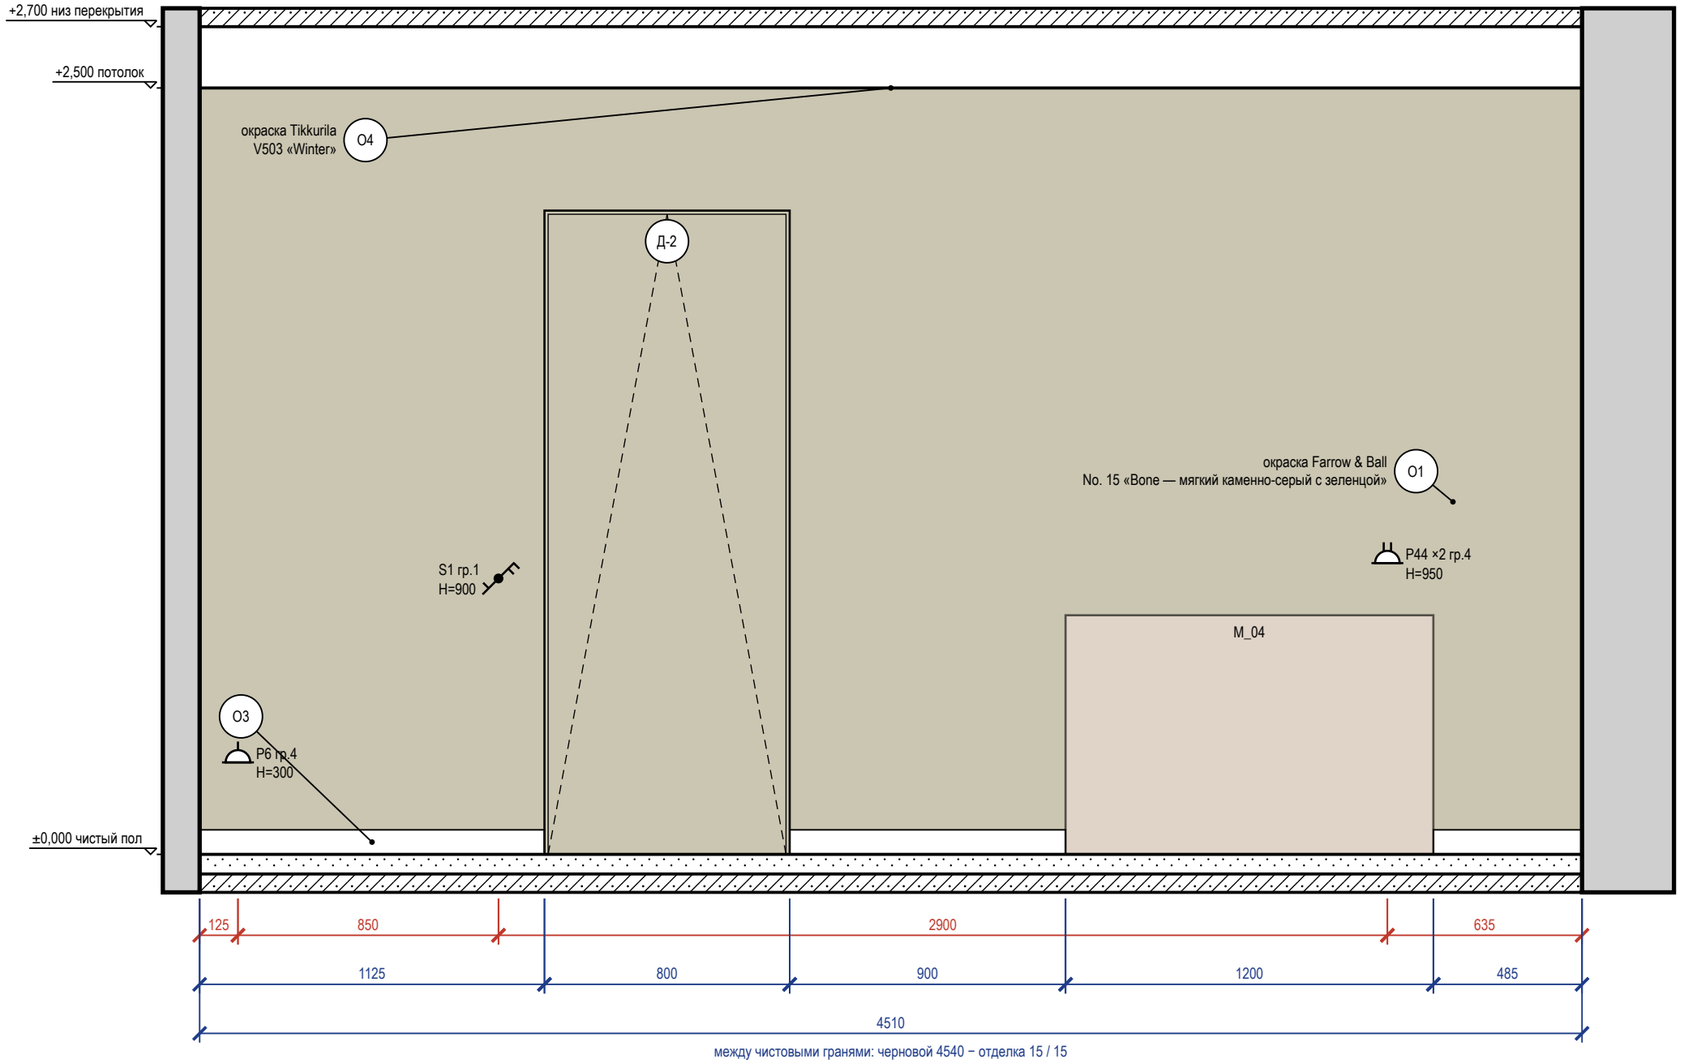


### Схема развёрток (М 1:100)

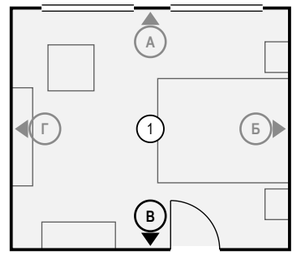


### Ведомость отделки (на листе)


| Марка | Поверхность | Материал, изделие | Цвет, код | Кол. |
|---|---|---|---|---|
| О1 | стены | окраска, Farrow & Ball Modern Emulsion, матовая, подготовка Q3 | Farrow & Ball No. 15 «Bone — мягкий каменно-серый с зеленцой» | 9,6 м² |
| О3 | плинтус | плинтус МДФ, h 80 мм, аналог: плинтус МДФ под покраску 80×16 | Farrow & Ball No. 15 «Bone — мягкий каменно-серый с зеленцой» | 2,5 м |
| О4 | потолок | окраска, Tikkurila Anti-Reflex 2, глубокоматовая, подготовка Q3 | Tikkurila V503 «Winter» | 17,9 м² |

### Примечания

1. Размеры — в мм от чистовых поверхностей стен; условные обозначения и общие указания — лист 27.
2. Двери скрытого монтажа — полотно в плоскости стены, отделка стены по полотну, плинтус прерывается у короба (узел — на листе узлов).
3. Потолок — у каждой стены свой, по плану потолков (ПТ1); ступени — зоной, кромка короба перед нишей — тонкой линией; в поле потолка: ПТ2 +2,600.


| | | | | | | |
|---|---|---|---|---|---|---|
| | | | | | Проект: Квартира с кабинетом | М 1:20 |
| | Лист | № док. | Подпись | Дата | | |
| Дизайнер | Кырлан А.С. | | | 04.11.26 | Развёртка стены В. Спальня (пом. 1) | Стадия: П; Лист: 78; Листов: 127 |

## Развёртка стены Г

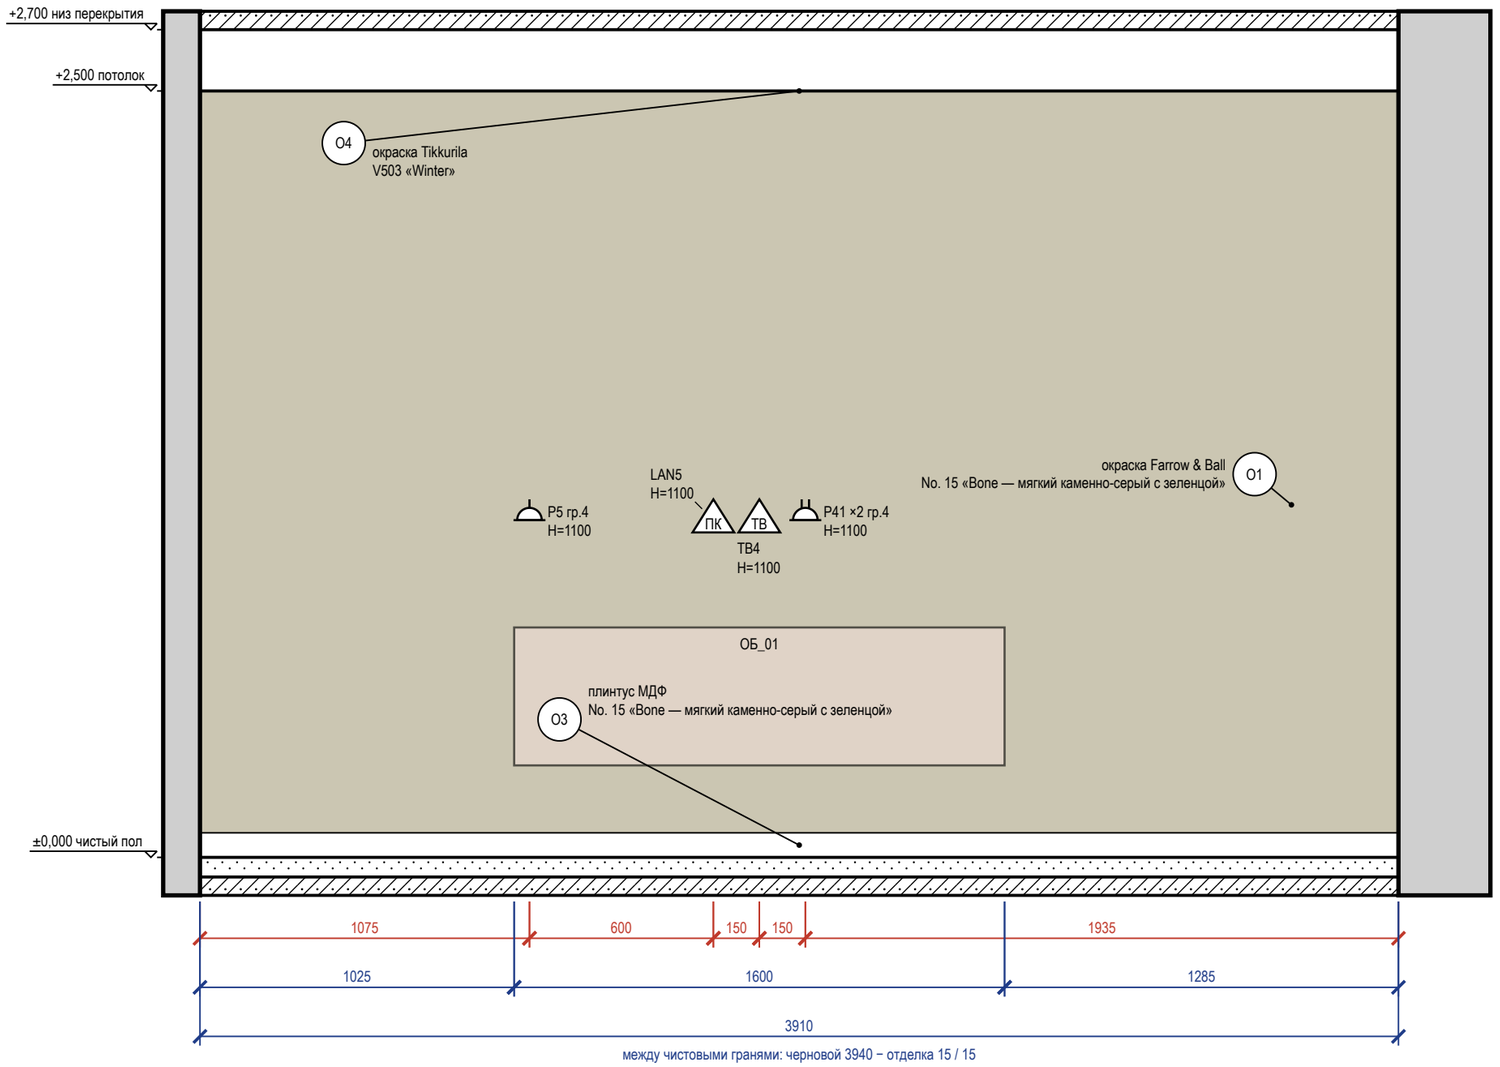


между чистовыми гранями: черновой 3940 − отделка 15 / 15

### Схема развёрток (М 1:100)

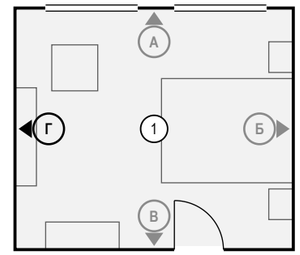


### Ведомость отделки (на листе)

| Марка | Поверхность | Материал, изделие | Цвет, код | Кол. |
|---|---|---|---|---|
| О1 | стены | окраска, Farrow & Ball Modern Emulsion, матовая, подготовка Q3 | Farrow & Ball No. 15 «Bone — мягкий каменно-серый с зеленцой» | 9,8 м² |
| О3 | плинтус | плинтус МДФ, h 80 мм, аналог: плинтус МДФ под покраску 80×16 | Farrow & Ball No. 15 «Bone — мягкий каменно-серый с зеленцой» | 3,9 м |
| О4 | потолок | окраска, Tikkurila Anti-Reflex 2, глубокоматовая, подготовка Q3 | Tikkurila V503 «Winter» | 17,9 м² |

Визуализация этой стены — лист 6




### Примечания


1. Размеры — в мм от чистовых поверхностей стен; условные обозначения и общие указания — лист 27.
2. Потолок — у каждой стены свой, по плану потолков (ПТ1); ступени — зоной, кромка короба перед нишей — тонкой линией; в поле потолка: ПТ2 +2,600.

| | | | | | |
|---|---|---|---|---|---|
| | | | | | Проект: Квартира с кабинетом — М 1:20 |
| | Лист | № док. | Подпись | Дата | Развёртка стены Г. Спальня (пом. 1) |
| Дизайнер | Кырлан А.С. | | | 04.11.26 | Стадия: П; Лист: 79; Листов: 127 |


## Развёртка стены А

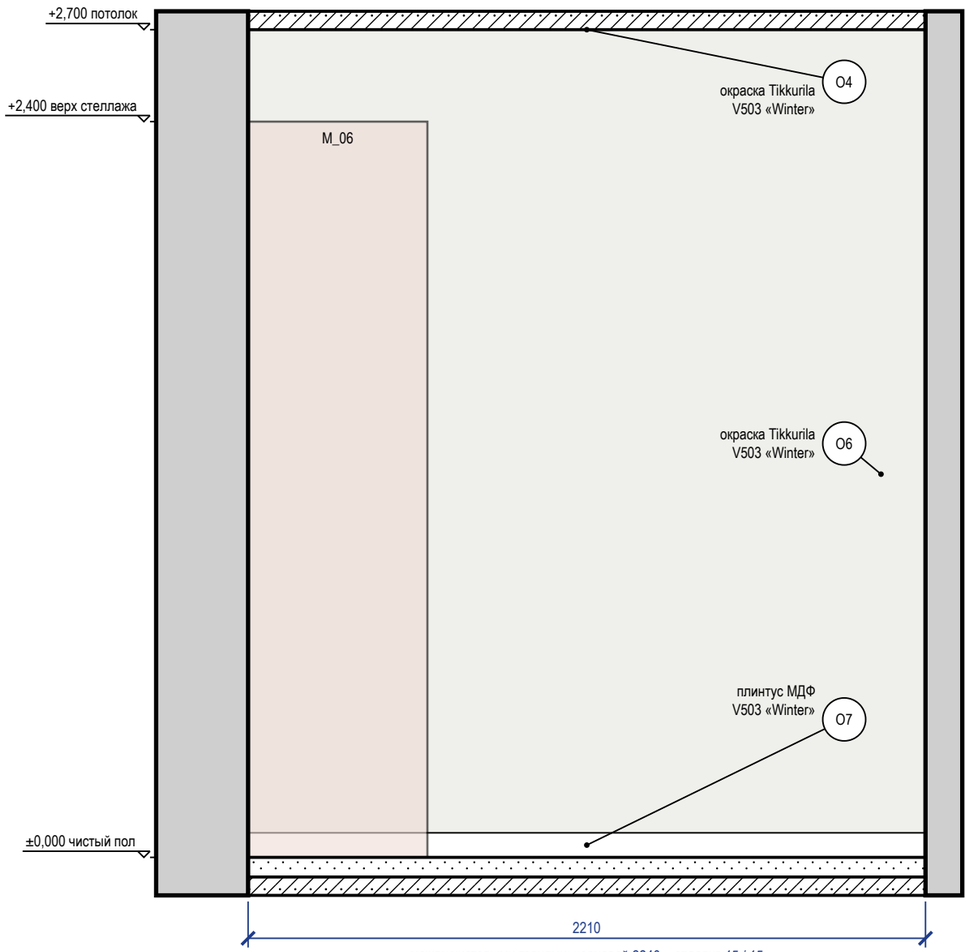


## Развёртка стены Б

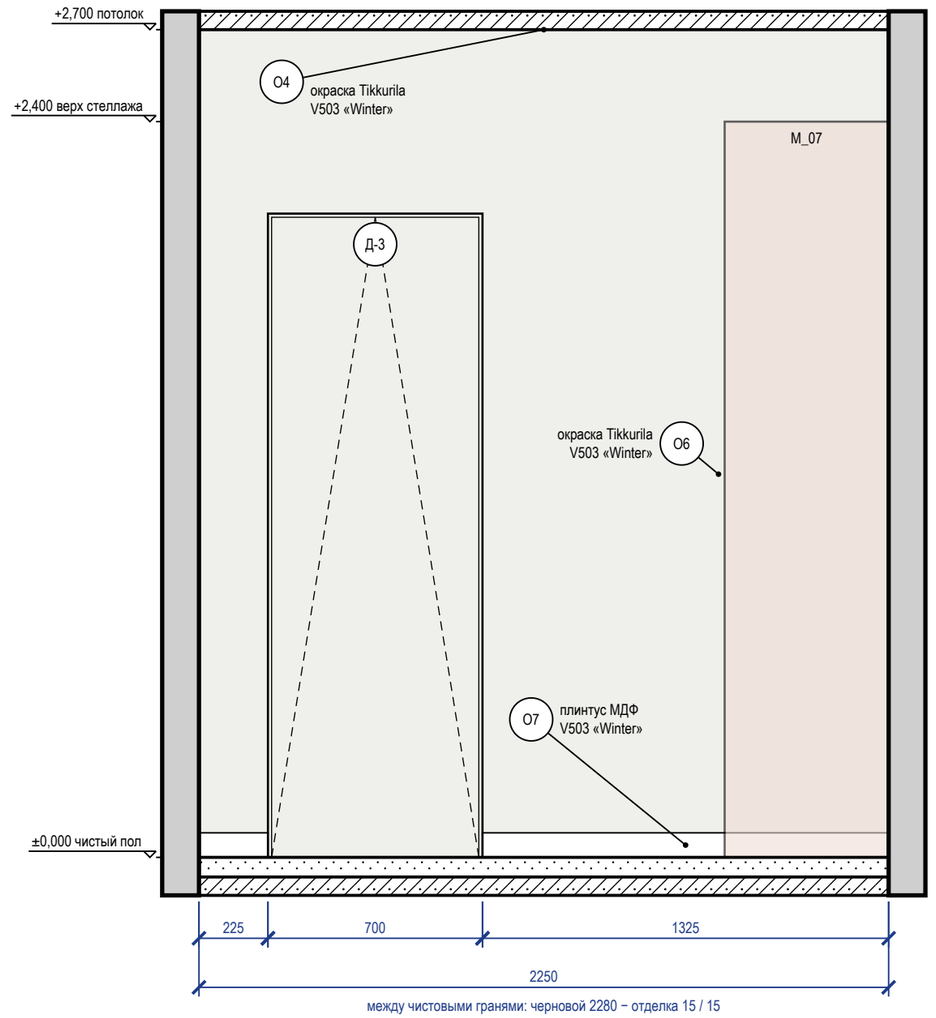


### Схема развёрток (М 1:100)

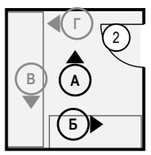


### Ведомость отделки (на листе)


| Марка | Поверхность | Материал, изделие | Цвет, код | Кол. |
|---|---|---|---|---|
| О4 | потолок | окраска, Tikkurila Anti-Reflex 2, глубокоматовая, подготовка Q3 | Tikkurila V503 «Winter» | 5,1 м² |
| О6 | стены | окраска, Tikkurila Harmony, матовая, подготовка Q3 | Tikkurila V503 «Winter» | 10,6 м² |
| О7 | плинтус | плинтус МДФ, h 80 мм, аналог: плинтус МДФ под покраску 80×16 | Tikkurila V503 «Winter» | 3,8 м |

### Примечания


1. Размеры — в мм от чистовых поверхностей стен; условные обозначения и общие указания — лист 27.
2. Двери скрытого монтажа — полотно в плоскости стены, отделка стены по полотну, плинтус прерывается у короба (узел — на листе узлов).

| | | | | | | |
|---|---|---|---|---|---|---|
| | | | | | Проект: Квартира с кабинетом | М 1:20 |
| | Лист | № док. | Подпись | Дата | Развёртки стен А, Б. Гардеробная-постирочная (пом. 2) | Стадия: П; Лист: 80; Листов: 127 |
| Дизайнер | Кырлан А.С. | | | 04.11.26 | | |


## Развёртка стены В

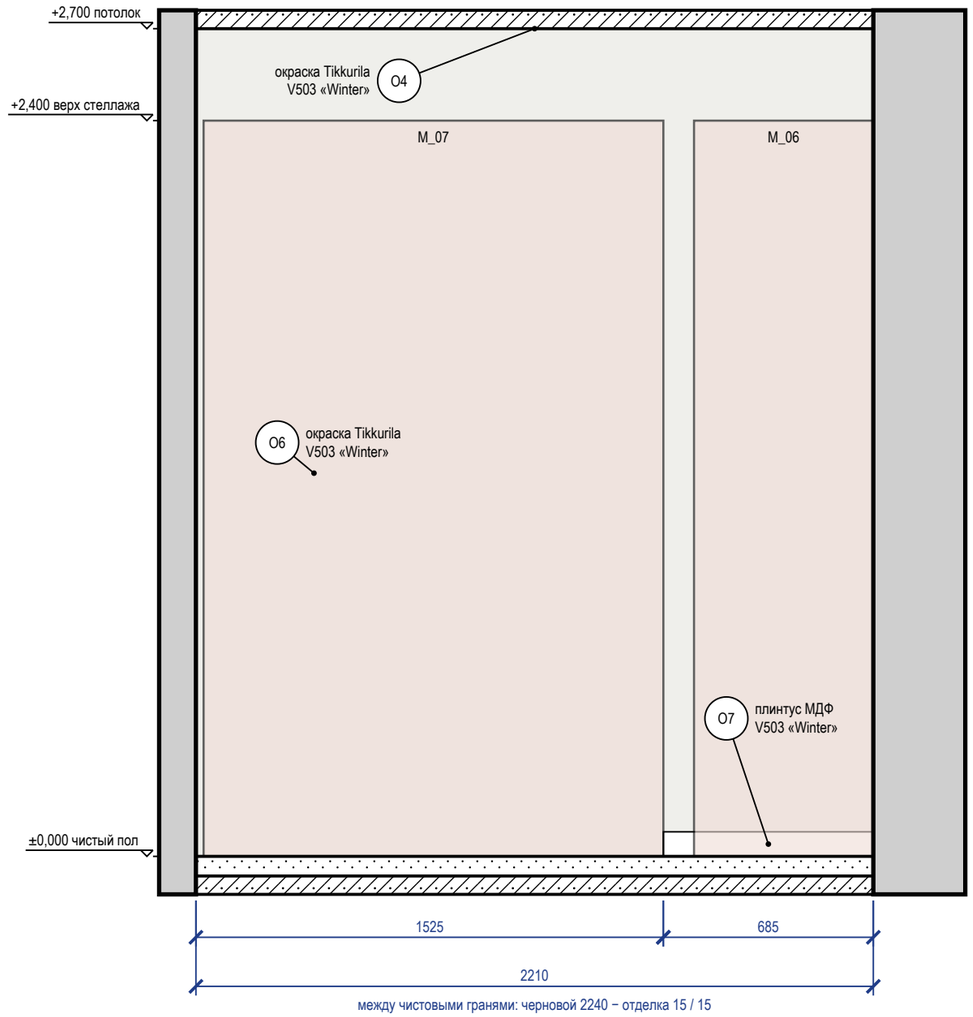


## Развёртка стены Г

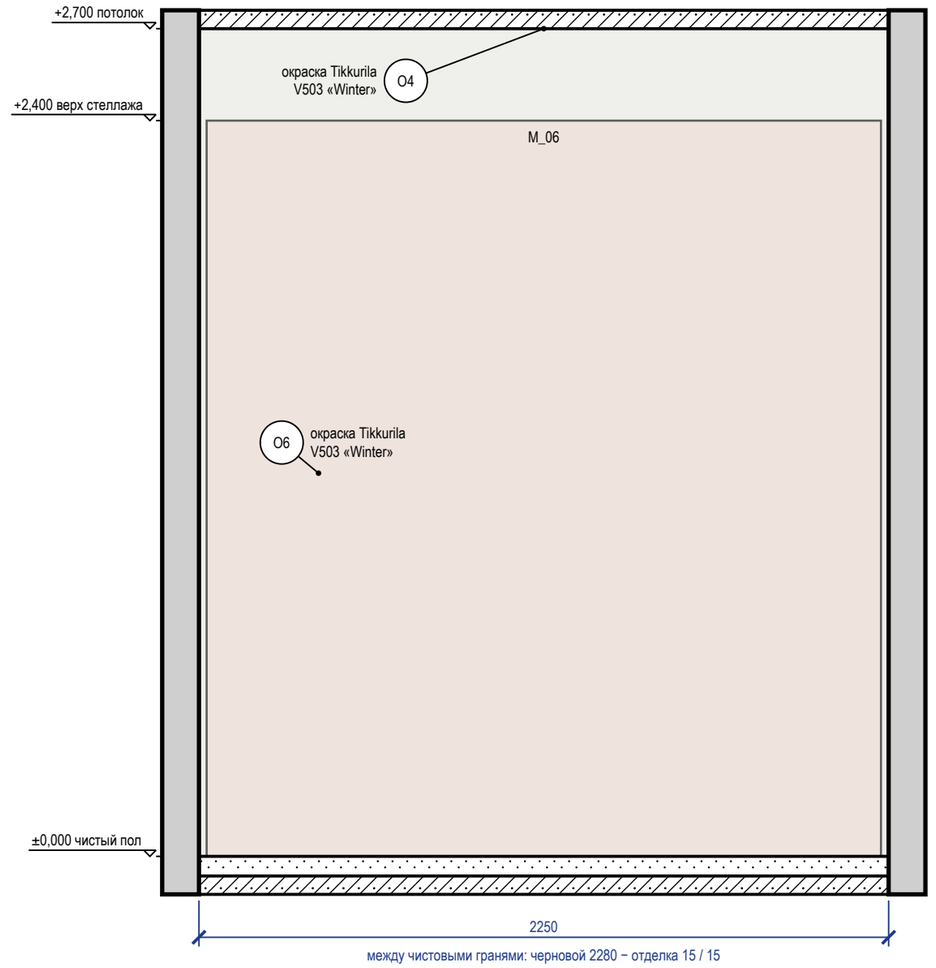


### Схема развёрток (М 1:100)

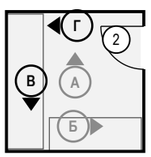


### Ведомость отделки (на листе)

| Марка | Поверхность | Материал, изделие | Цвет, код | Кол. |
|---|---|---|---|---|
| O4 | потолок | окраска, Tikkurila Anti-Reflex 2, глубокоматовая, подготовка Q3 | Tikkurila V503 «Winter» | 5,1 м² |
| O6 | стены | окраска, Tikkurila Harmony, матовая, подготовка Q3 | Tikkurila V503 «Winter» | 12 м² |
| O7 | плинтус | плинтус МДФ, h 80 мм, аналог: плинтус МДФ под покраску 80×16 | Tikkurila V503 «Winter» | 0,7 м |

Визуализация этой стены — лист 7




### Примечания

1. Размеры — в мм от чистовых поверхностей стен; условные обозначения и общие указания — лист 27.


| | | | | | | |
|---|---|---|---|---|---|---|
| | | | | | Проект: Квартира с кабинетом | М 1:20 |
| | Лист | № док. | Подпись | Дата | | |
| Дизайнер | Кырлан А.С. | | | 04.11.26 | Развёртки стен В, Г. Гардеробная-постирочная (пом. 2) | Стадия: П; Лист: 81; Листов: 127 |

выпуск 04.11.2026 № 627e1ac6ce · стр. 81 из 127

## Развёртка стены А

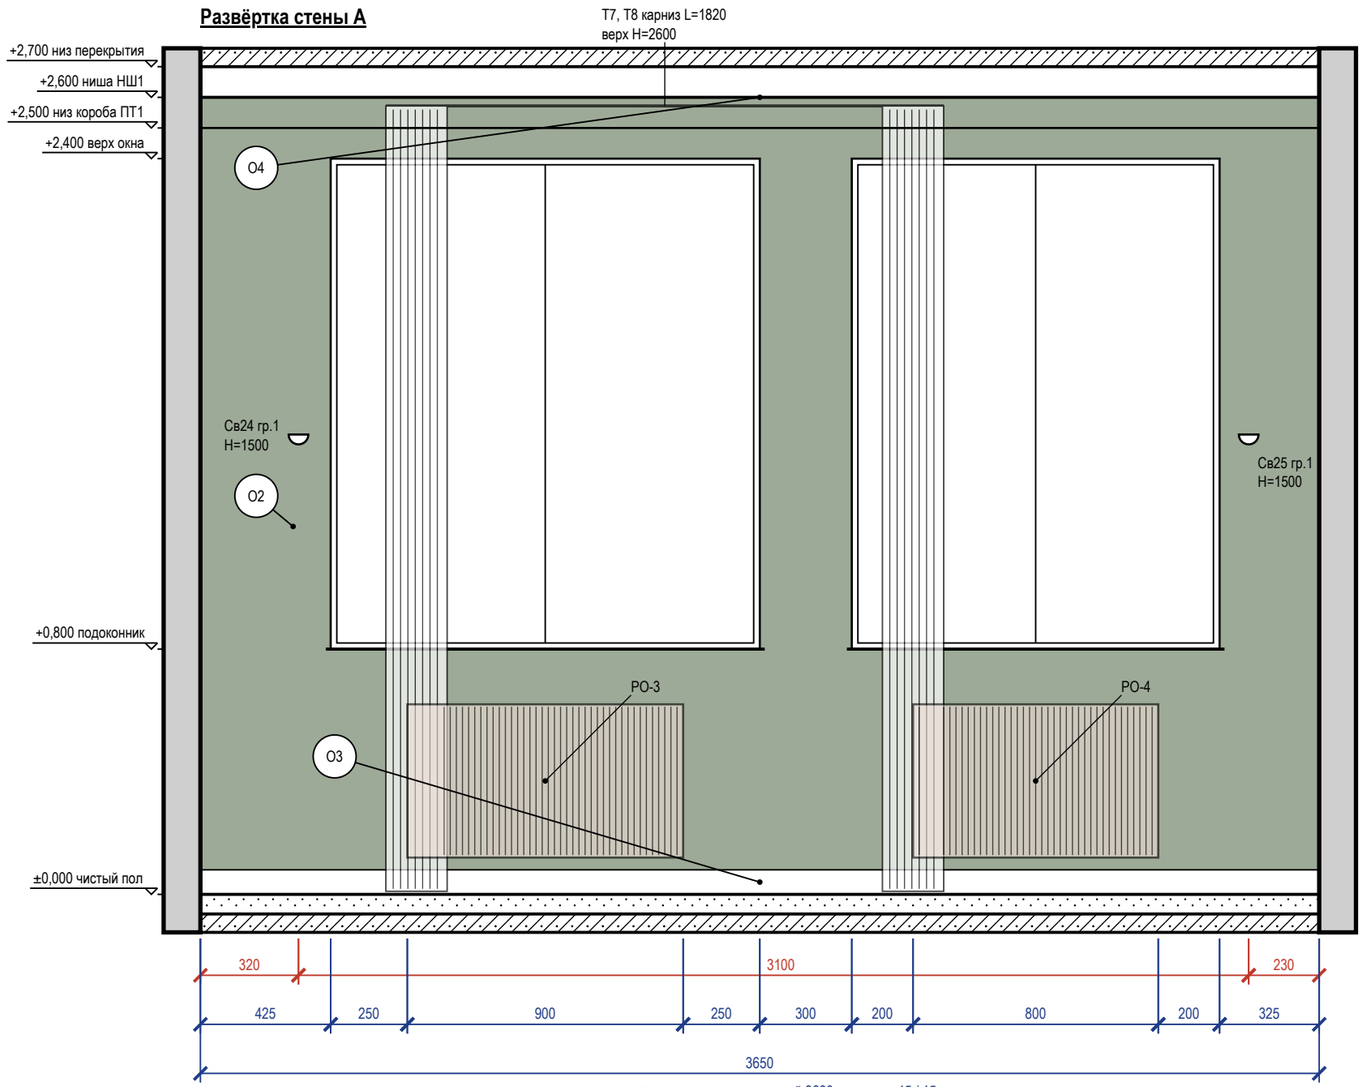


## Схема развёрток (М 1:100)

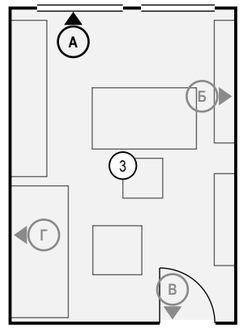


## Ведомость отделки (на листе)

| Марка | Поверхность | Материал, изделие | Цвет, код | Кол. |
|---|---|---|---|---|
| О2 | акцентная стена | окраска, Farrow & Ball Modern Emulsion, матовая, подготовка Q3 | Farrow & Ball No. 34 «Calke Green традиционный шалфей» | 5,3 м² |
| О3 | плинтус | плинтус МДФ, h 80 мм, аналог: плинтус МДФ под покраску 80×16 | Farrow & Ball No. 15 «Bone — мягкий каменно-серый с зеленцой» | 3,6 м |
| О4 | потолок | окраска, Tikkurila Anti-Reflex 2, глубокоматовая, подготовка Q3 | Tikkurila V503 «Winter» | 18,9 м² |

Визуализация этой стены — лист 8




## Примечания


1. Размеры — в мм от чистовых поверхностей стен; условные обозначения и общие указания — лист 27.
2. Карнизы (шины) — по ведомости текстиля декоратора: длина L и верх H на развёртке — те же числа, что в ведомости; крепление — до окраски потолка.
3. Потолок — у каждой стены свой, по плану потолков (НШ1, ПТ1); ступени — зоной, кромка короба перед нишей — тонкой линией; в поле потолка: ПТ2 +2,600.
4. Линии узора (швы плитки, складки штор, рёбра радиаторов) прерываются у знаков и выносок — просвет между линиями не менее 0,7 мм.

| | | | | | | |
|---|---|---|---|---|---|---|
| | | | | | Проект: Квартира с кабинетом | М 1:20 |
| | Лист | № док. | Подпись | Дата | Развёртка стены А. Кабинет (пом. 3) | Стадия: П; Лист: 82; Листов: 127 |
| Дизайнер | Кырлан А.С. | | | 04.11.26 | | |

## Развёртка стены Б

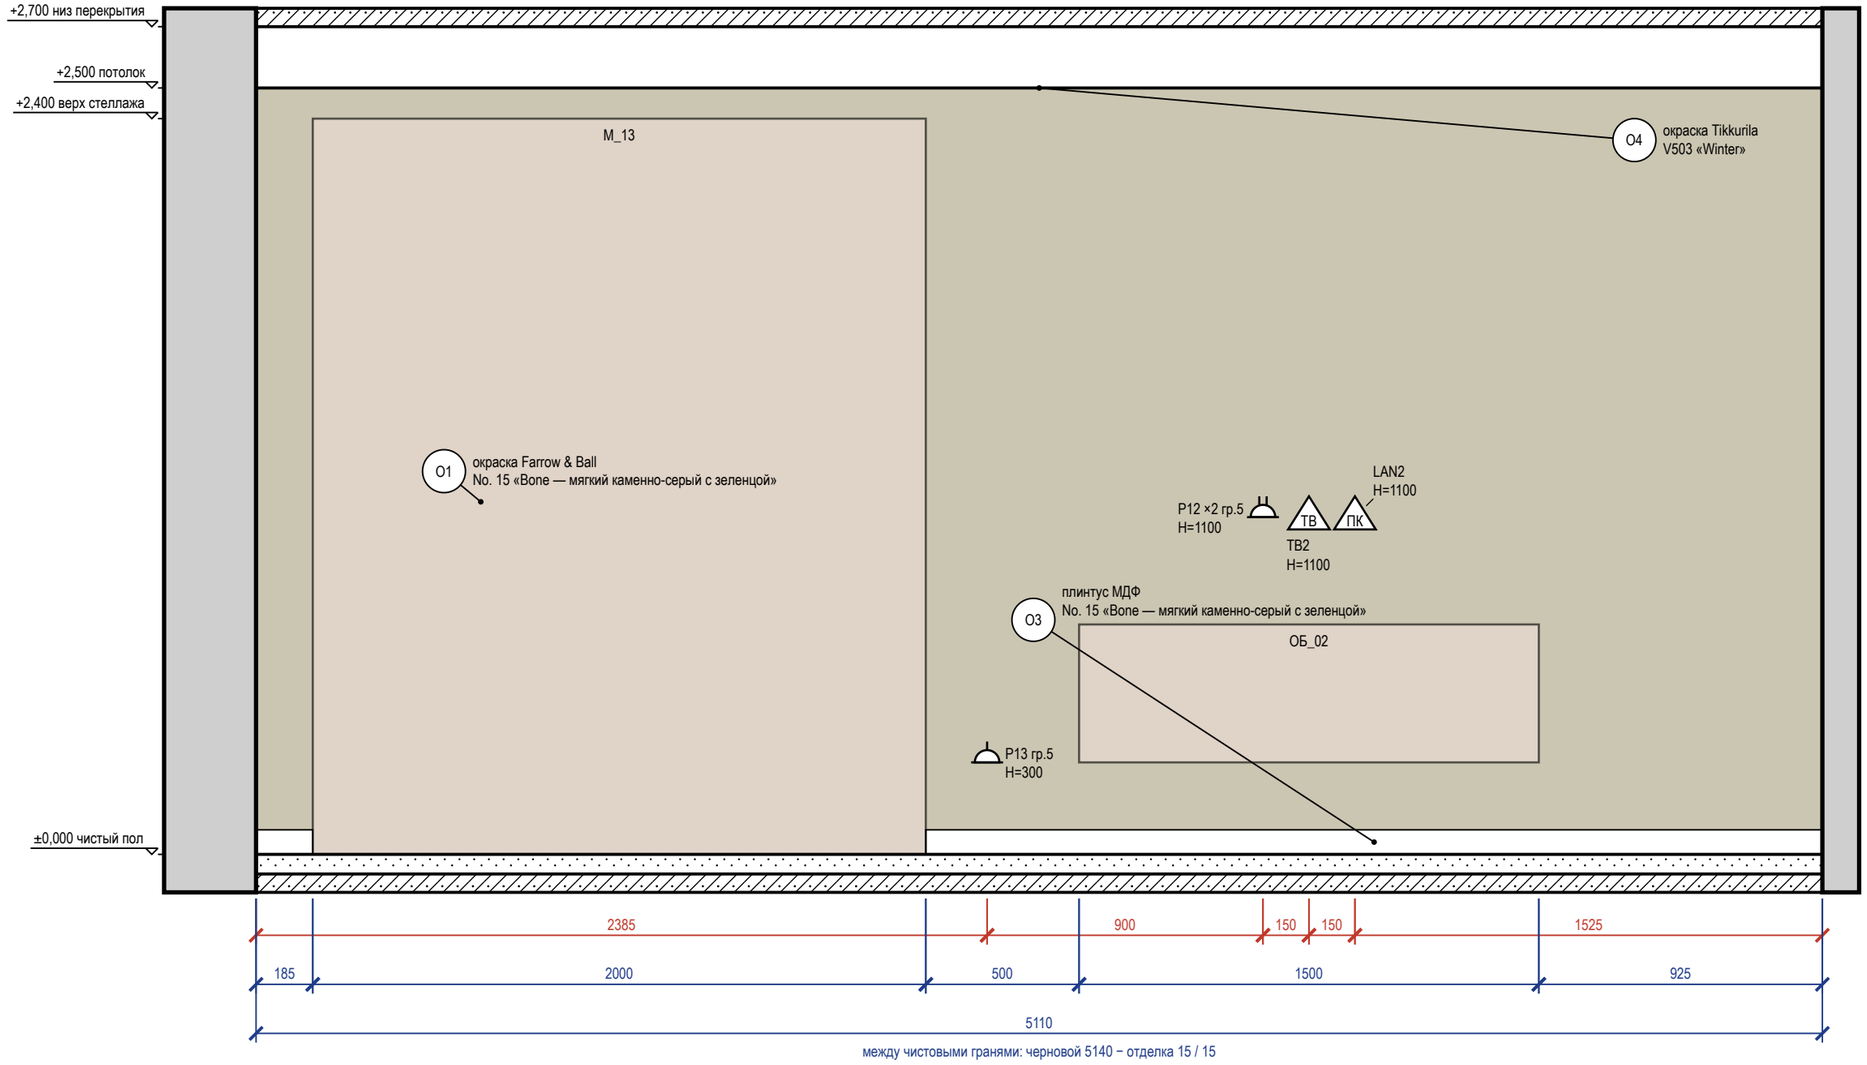


### Схема развёрток (М 1:100)

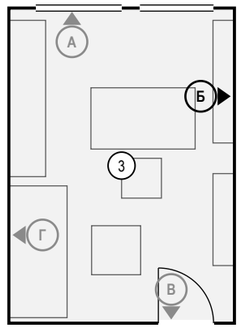


### Ведомость отделки (на листе)

| Марка | Поверхность | Материал, изделие | Цвет, код | Кол. |
|---|---|---|---|---|
| О1 | стены | окраска, Farrow & Ball Modern Emulsion, матовая, подготовка Q3 | Farrow & Ball No. 15 «Bone — мягкий каменно-серый с зеленцой» | 12,8 м² |
| О3 | плинтус | плинтус МДФ, h 80 мм, аналог: плинтус МДФ под покраску 80×16 | Farrow & Ball No. 15 «Bone — мягкий каменно-серый с зеленцой» | 3,1 м |
| О4 | потолок | окраска, Tikkurila Anti-Reflex 2, глубокоматовая, подготовка Q3 | Tikkurila V503 «Winter» | 18,9 м² |

Визуализация этой стены — лист 9



### Примечания

1. Размеры — в мм от чистовых поверхностей стен; условные обозначения и общие указания — лист 27.
2. Потолок — у каждой стены свой, по плану потолков (ПТ1); ступени — зоной, кромка короба перед нишей — тонкой линией; в поле потолка: ПТ2 +2,600.

| | | | | |
|---|---|---|---|---|
| | Лист | № док. | Подпись | Дата |
| Дизайнер | Кырлан А.С. | | | 04.11.26 |


Проект: Квартира с кабинетом — М 1:20

Развёртка стены Б. Кабинет (пом. 3)

| Стадия | Лист | Листов |
|---|---|---|
| П | 83 | 127 |


выпуск 04.11.2026 № 627e1ac6ce · стр. 83 из 127

## Развёртка стены В

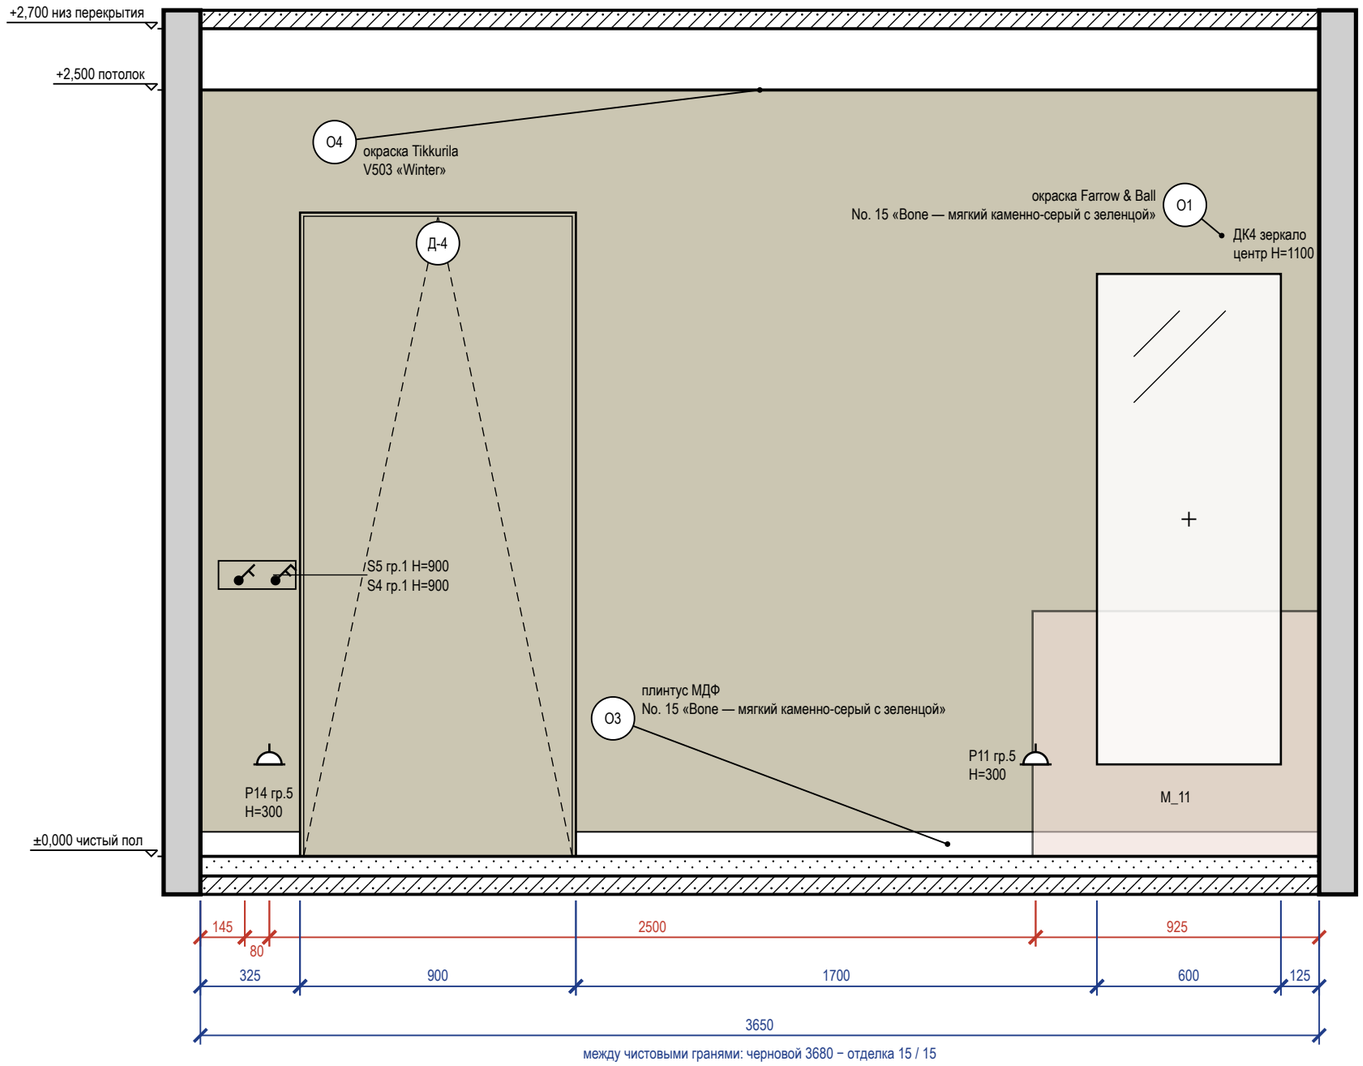


между чистовыми гранями: черновой 3680 − отделка 15 / 15

### Схема развёрток (М 1:100)

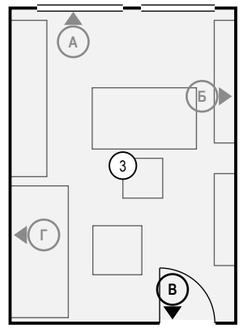


### Ведомость отделки (на листе)

| Марка | Поверхность | Материал, изделие | Цвет, код | Кол. |
|---|---|---|---|---|
| О1 | стены | окраска, Farrow & Ball Modern Emulsion, матовая, подготовка Q3 | Farrow & Ball No. 15 «Bone — мягкий каменно-серый с зеленцой» | 7,2 м² |
| О3 | плинтус | плинтус МДФ, h 80 мм, аналог: плинтус МДФ под покраску 80×16 | Farrow & Ball No. 15 «Bone — мягкий каменно-серый с зеленцой» | 2,8 м |
| О4 | потолок | окраска, Tikkurila Anti-Reflex 2, глубокоматовая, подготовка Q3 | Tikkurila V503 «Winter» | 18,9 м² |

### Примечания

1. Размеры — в мм от чистовых поверхностей стен; условные обозначения и общие указания — лист 27.
2. Картины и зеркала крепить к основанию по паспорту изделия (закладные и анкеры — в перечне скрытых работ); крест — ось центра предмета.
3. Двери скрытого монтажа — полотно в плоскости стены, отделка стены по полотну, плинтус прерывается у короба (узел — на листе узлов).
4. Потолок — у каждой стены свой, по плану потолков (ПТ1); ступени — зоной, кромка короба перед нишей — тонкой линией; в поле потолка: ПТ2 +2,600.


| | | | | |
|---|---|---|---|---|
| | Лист | № док. | Подпись | Дата |
| Дизайнер | Кырлан А.С. | | | 04.11.26 |

Проект: Квартира с кабинетом — **М 1:20**


Развёртка стены В. Кабинет (пом. 3)

| Стадия | Лист | Листов |
|---|---|---|
| П | 84 | 127 |

## Развёртка стены Г

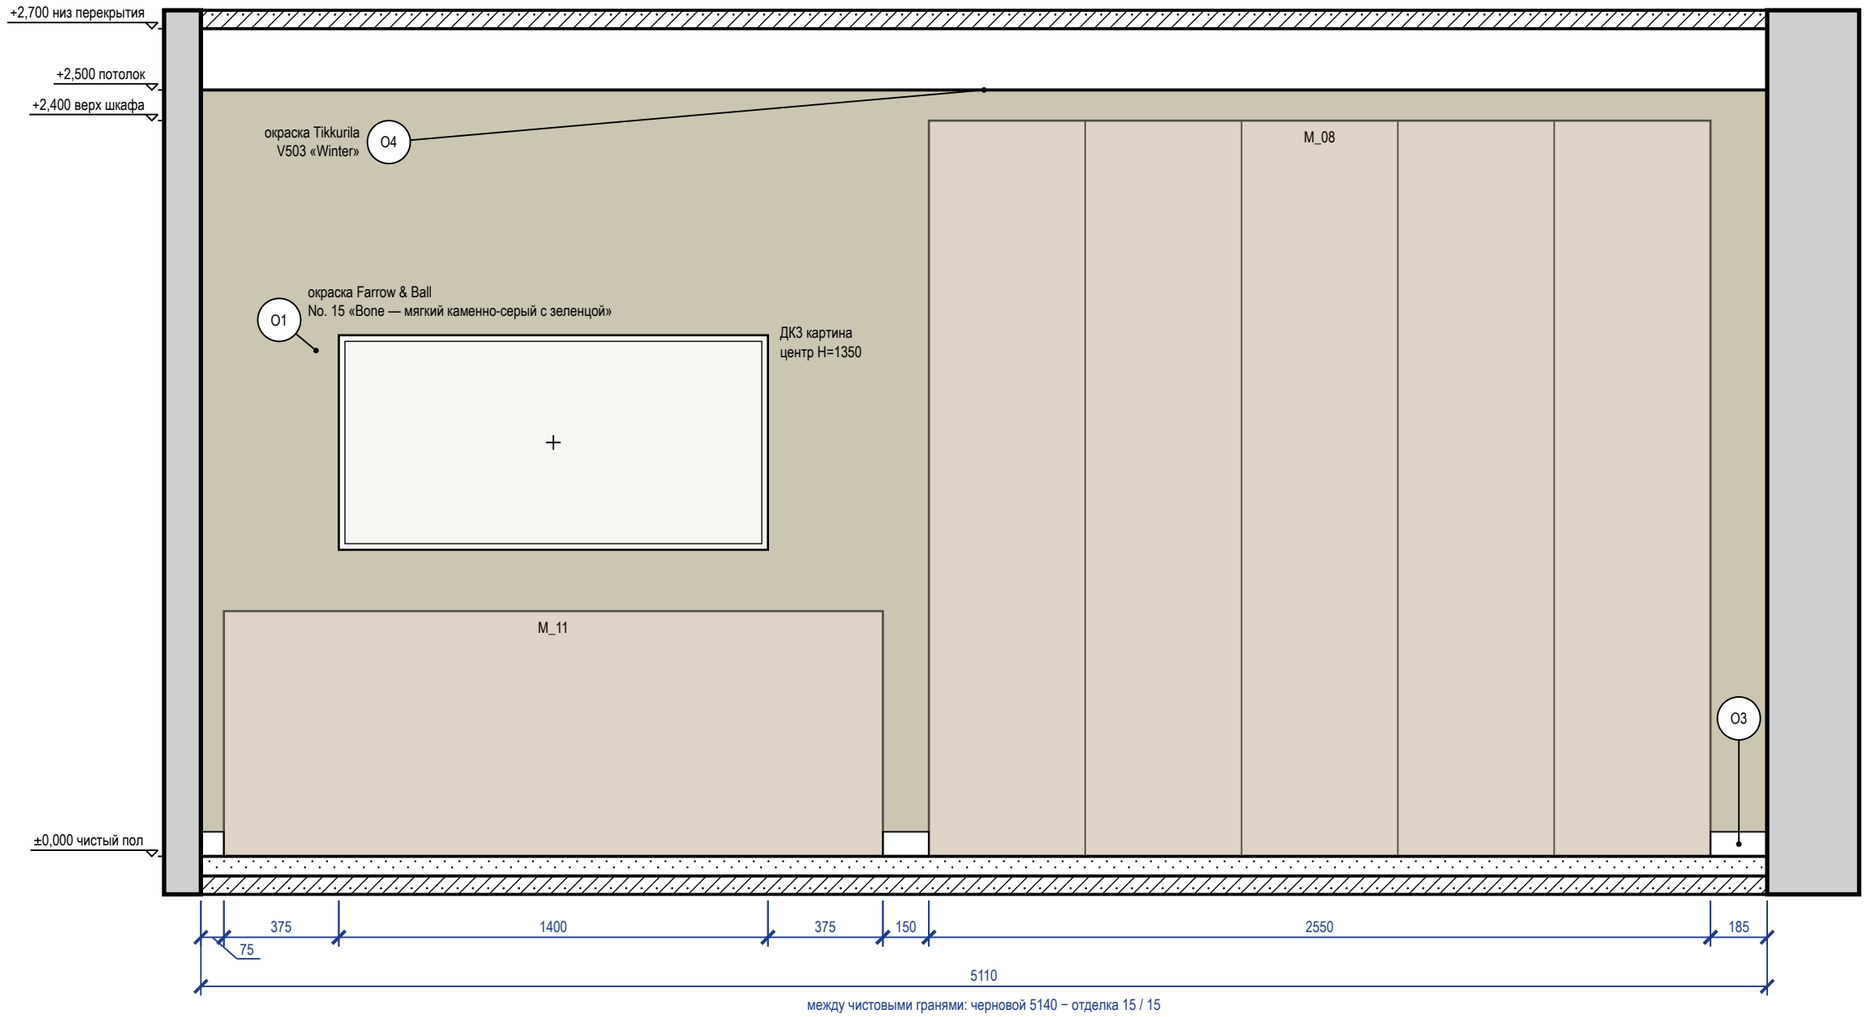



### Схема развёрток (М 1:100)

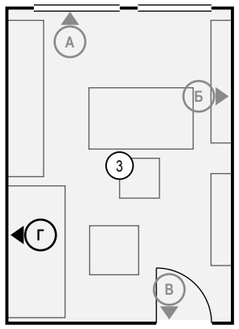


### Ведомость отделки (на листе)

| Марка | Поверхность | Материал, изделие | Цвет, код | Кол. |
|---|---|---|---|---|
| O1 | стены | окраска, Farrow & Ball Modern Emulsion, матовая, подготовка Q3 | Farrow & Ball No. 15 «Bone — мягкий каменно-серый с зеленцой» | 12,8 м² |
| O3 | плинтус | плинтус МДФ, h 80 мм, аналог: плинтус МДФ под покраску 80×16 | Farrow & Ball No. 15 «Bone — мягкий каменно-серый с зеленцой» | 0,4 м |
| O4 | потолок | окраска, Tikkurila Anti-Reflex 2, глубокоматовая, подготовка Q3 | Tikkurila V503 «Winter» | 18,9 м² |

Визуализация этой стены — лист 10

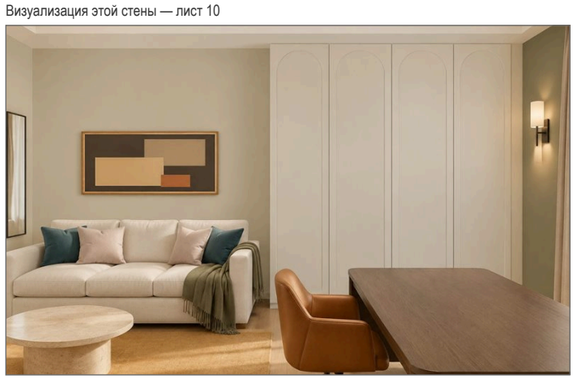


### Примечания

1. Размеры — в мм от чистовых поверхностей стен; условные обозначения и общие указания — лист 27.
2. Картины и зеркала крепить к основанию по паспорту изделия (закладные и анкеры — в перечне скрытых работ); крест — ось центра предмета.
3. Потолок — у каждой стены свой, по плану потолков (ПТ1); ступени — зоной, кромка короба перед нишей — тонкой линией; в поле потолка: ПТ2 +2,600.


| | | | | | | |
|---|---|---|---|---|---|---|
| | | | | | Проект: Квартира с кабинетом | М 1:20 |
| | Лист | № док. | Подпись | Дата | Развёртка стены Г. Кабинет (пом. 3) | Стадия: П; Лист: 85; Листов: 127 |
| Дизайнер | Кырлан А.С. | | | 04.11.26 | | |

выпуск 04.11.2026 № 627e1ac6ce · стр. 85 из 127

## Развёртка стены Г

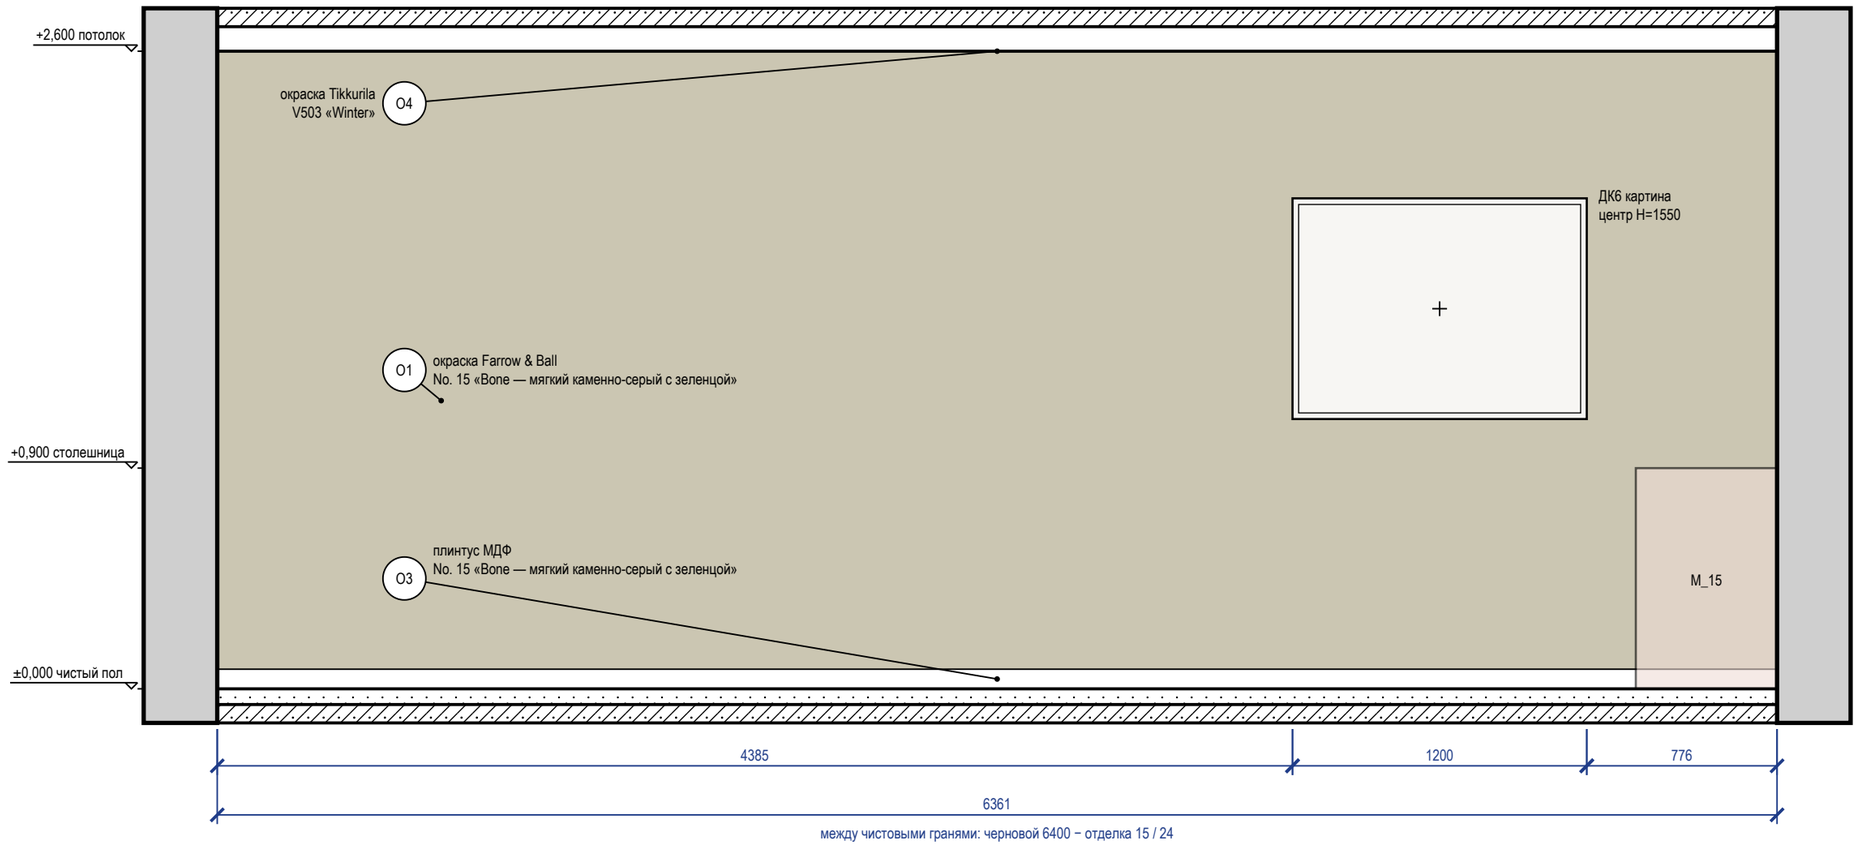


### Схема развёрток (М 1:100)

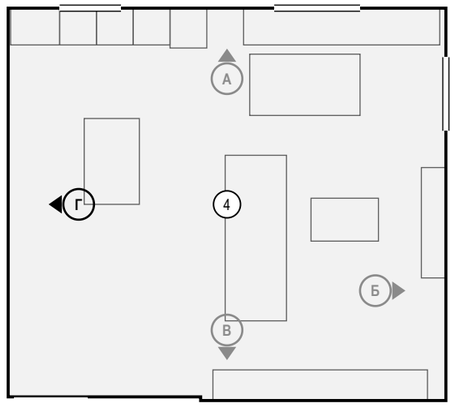


### Ведомость отделки (на листе)

| Марка | Поверхность | Материал, изделие | Цвет, код | Кол. |
|---|---|---|---|---|
| O1 | стены | окраска, Farrow & Ball Modern Emulsion, матовая, подготовка Q3 | Farrow & Ball No. 15 «Bone — мягкий каменно-серый с зеленцой» | 16,5 м² |
| O3 | плинтус | плинтус МДФ, h 80 мм, аналог: плинтус МДФ под покраску 80×16 | Farrow & Ball No. 15 «Bone — мягкий каменно-серый с зеленцой» | 6,4 м |
| O4 | потолок | окраска, Tikkurila Anti-Reflex 2, глубокоматовая, подготовка Q3 | Tikkurila V503 «Winter» | 45,5 м² |

Визуализация этой стены — лист 14




### Примечания

1. Размеры — в мм от чистовых поверхностей стен; условные обозначения и общие указания — лист 27.
2. Стена Г показана двумя видами: здесь — архитектурная развёртка (мебель, отделка, проёмы, высоты), электроточки и выводы ВК с привязками и таблицей — на листе 87 («Привязки»).
3. Картины и зеркала крепить к основанию по паспорту изделия (закладные и анкеры — в перечне скрытых работ); крест — ось центра предмета.
4. Потолок — у каждой стены свой, по плану потолков (ПТ2); ступени — зоной, кромка короба перед нишей — тонкой линией; в поле потолка: ПТ1 +2,500.

| | | | | | | | |
|---|---|---|---|---|---|---|---|
| | | | | | Проект: Квартира с кабинетом | | М 1:25 |
| | Лист | № док. | Подпись | Дата | | | |
| Дизайнер | Кырлан А.С. | | | 04.11.26 | Развёртка стены Г. Кухня-гостиная (пом. 4), кухонный фронт | Стадия | Лист | Листов |
| | | | | | | П | 86 | 127 |

## Развёртка стены Г: электроточки и выводы

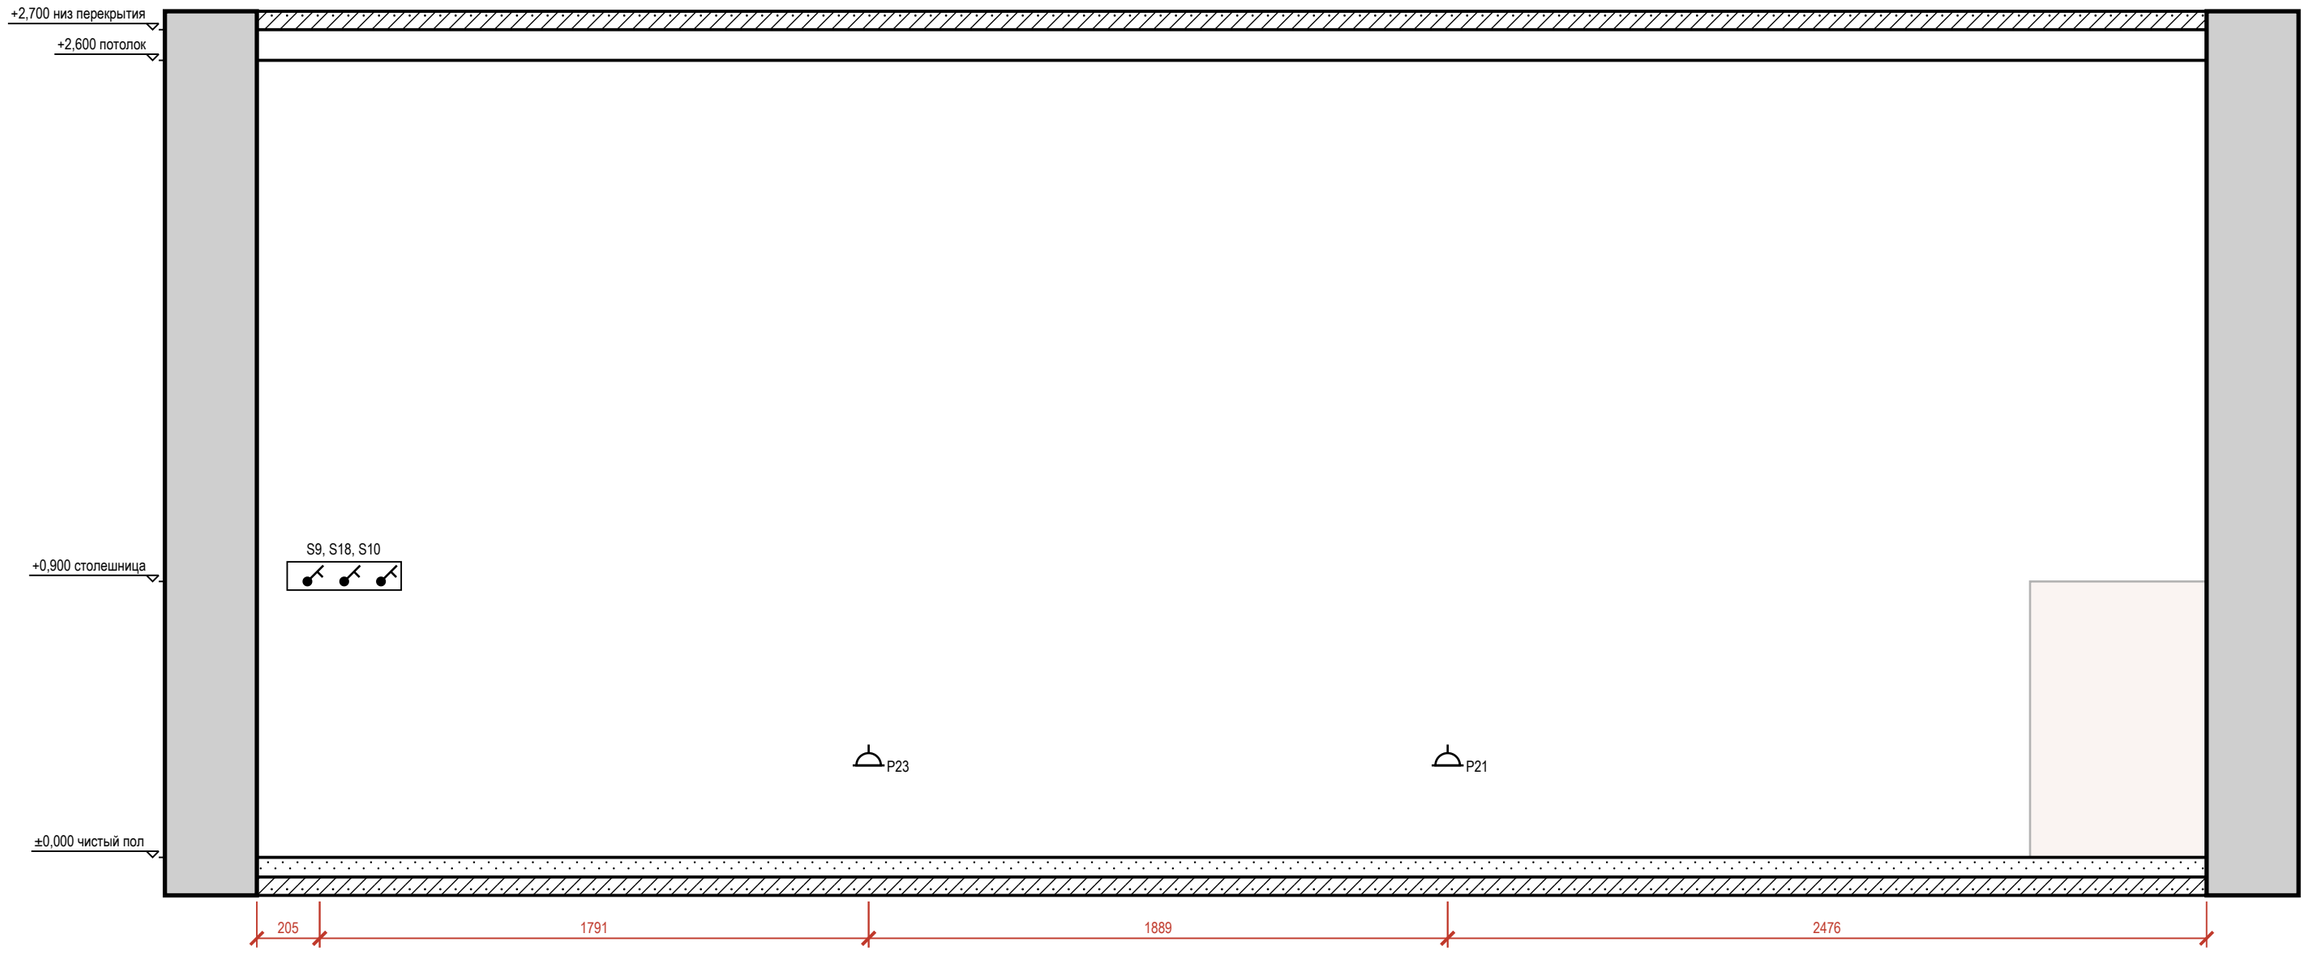



### Таблица привязок электроточек и выводов

| Марка | Назначение | От угла, мм | H от пола, мм | Примечание |
|---|---|---|---|---|
| S9 | выключатель | 205 | 900 | гр. 2 |
| S18 | выключатель | 285 | 900 | гр. 2 |
| S10 | выключатель | 365 | 900 | гр. 2 |
| P23 | розетка: уборка, пылесос | 1996 | 300 | гр. 6 |
| P21 | розетка: общего назначения | 3885 | 300 | гр. 6 |

### Условные обозначения

- розетка с заземляющим контактом; у знака — марка, ×N постов в рамке, гр. — группа щита, H — высота оси, мм
- выключатель одноклавишный
- привязки точек и выводов от угла и от пола, мм
- А — марка развёртки: буква стены, стрелка — взгляд

### Схема развёрток (М 1:200)

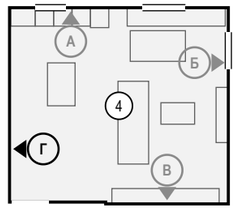



### Примечания

1. Вид «Привязки» стены Г — электроточки и выводы ВК; архитектурная развёртка (мебель, отделка, проёмы, высоты) — на листе 86. Мебель и приборы — подложкой для ориентира; их марки и обозначения мебели, проёмов и стен — там же.
2. Привязки — в мм: по горизонтали от левого чистового угла стены до оси изделия, H — от чистого пола до оси; все точки — в таблице привязок. Красная цепочка — привязки по осям; точки ближе 120 мм одна к другой в цепочку не дробятся — их привязки только в таблице.
3. У знака — марка электроточки (Р — розетка, S — выключатель, Св — светильник, ЭВ — вывод кабеля); условные обозначения и общие указания — лист 27.
4. Выводы кухонной техники — по утверждённому проекту кухни: привязки выводов даются от осей модулей гарнитура.


| | | | | | |
|---|---|---|---|---|---|
| | | | | | Проект: Квартира с кабинетом — М 1:20 |
| | Лист | № док. | Подпись | Дата | |
| Дизайнер | Кырлан А.С. | | | 04.11.26 | Привязки электроточек, стена Г. Кухня-гостиная (пом. 4) |

| Стадия | Лист | Листов |
|---|---|---|
| П | 87 | 127 |

## Развёртка стены А

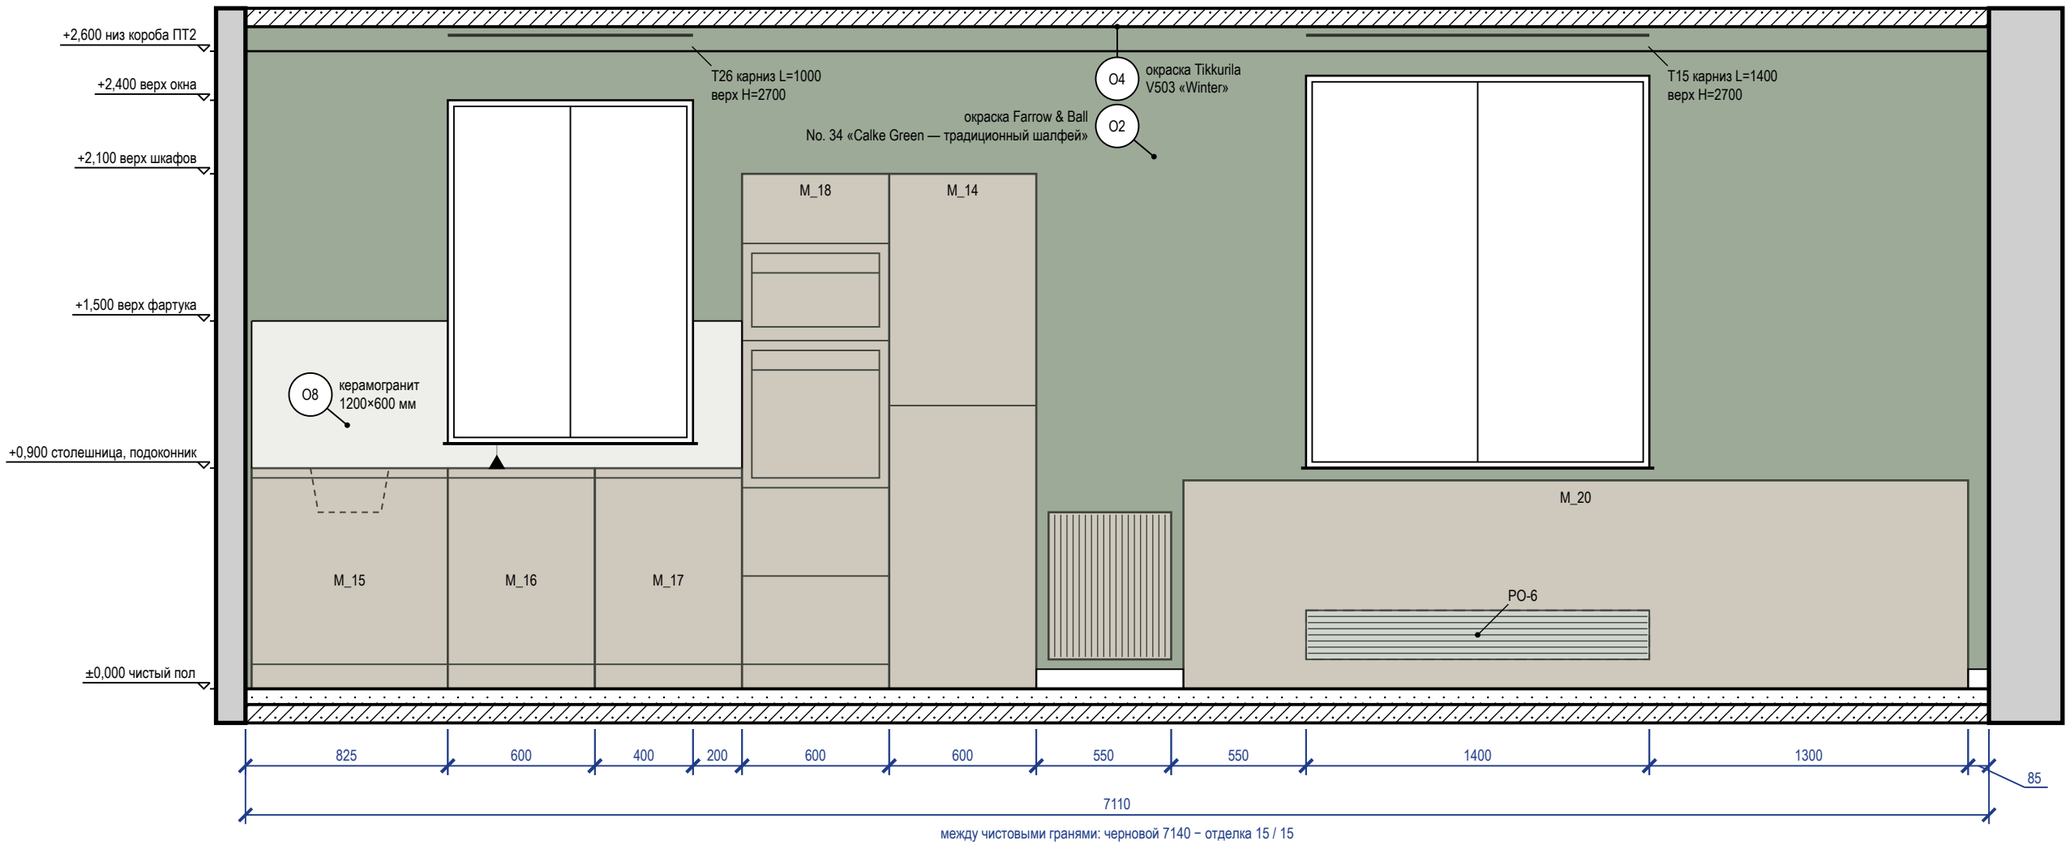



### Схема развёрток (М 1:100)

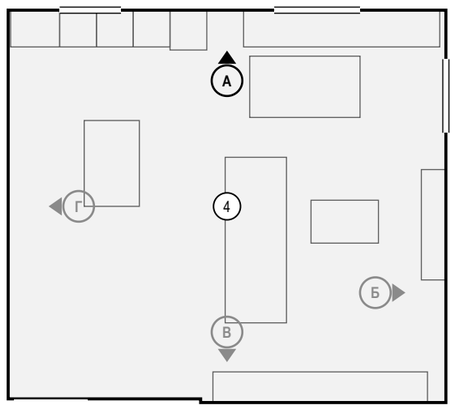


### Ведомость отделки (на листе)

| Марка | Поверхность | Материал, изделие | Цвет, код | Кол. |
|---|---|---|---|---|
| О2 | акцентная стена | окраска, Farrow & Ball Modern Emulsion, матовая, подготовка Q3 | Farrow & Ball No. 34 «Calke Green традиционный шалфей» | 14,4 м² |
| О3 | плинтус | плинтус МДФ, h 80 мм, аналог: плинтус МДФ под покраску 80×16 | Farrow & Ball No. 15 «Bone — мягкий каменно-серый с зеленцой» | 0,7 м |
| О4 | потолок | окраска, Tikkurila Anti-Reflex 2, глубокоматовая, подготовка Q3 | Tikkurila V503 «Winter» | 45,5 м² |
| О8 | фартук | керамогранит, 1200×600×9 мм, аналог: керамогранит под травертин, матовый, затирка CG2WA | | 0,7 м² |

Визуализация этой стены — лист 11

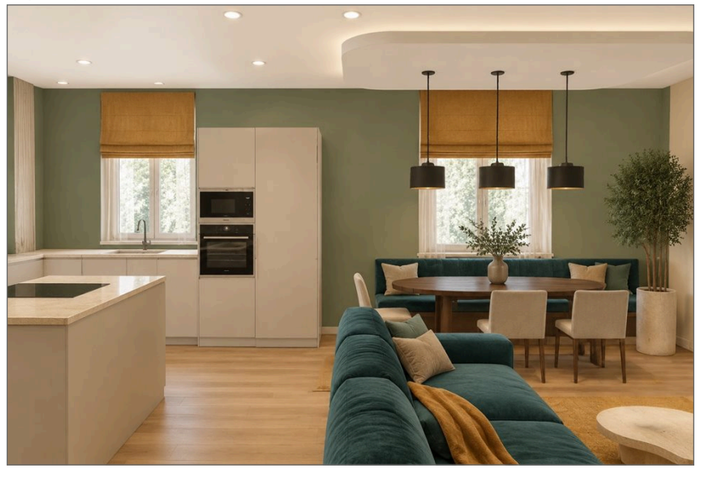


### Примечания

1. Размеры — в мм от чистовых поверхностей стен; условные обозначения и общие указания — лист 27.
2. Стена А показана двумя видами: здесь — архитектурная развёртка (мебель, отделка, проёмы, высоты), электроточки и выводы ВК с привязками и таблицей — на листе 89 («Привязки»).
3. Радиатор за корпусом мебели — штриховой линией; горизонтальные ламели — решётка экрана в лицевой панели по ширине прибора, щель для тёплого воздуха над прибором — по чертежу изделия.
4. Карнизы (шины) — по ведомости текстиля декоратора: длина L и верх H на развёртке — те же числа, что в ведомости; крепление — до окраски потолка.
5. Высота фартука принята 600 мм над столешницей там, где нет навесных модулей и высота фартука не задана.
6. Потолок — у каждой стены свой, по плану потолков (НШ2, ПТ2); ступени — зоной, кромка короба перед нишей — тонкой линией; в поле потолка: ПТ1 +2,500.

| | | | | | |
|---|---|---|---|---|---|
| | | | | | Проект: Квартира с кабинетом — М 1:25 |
| | Лист | № док. | Подпись | Дата | Развёртка стены А. Кухня-гостиная (пом. 4), кухонный фронт |
| Дизайнер | Кырлан А.С. | | | 04.11.26 | Стадия: П; Лист: 88; Листов: 127 |

## Развёртка стены А: электроточки и выводы

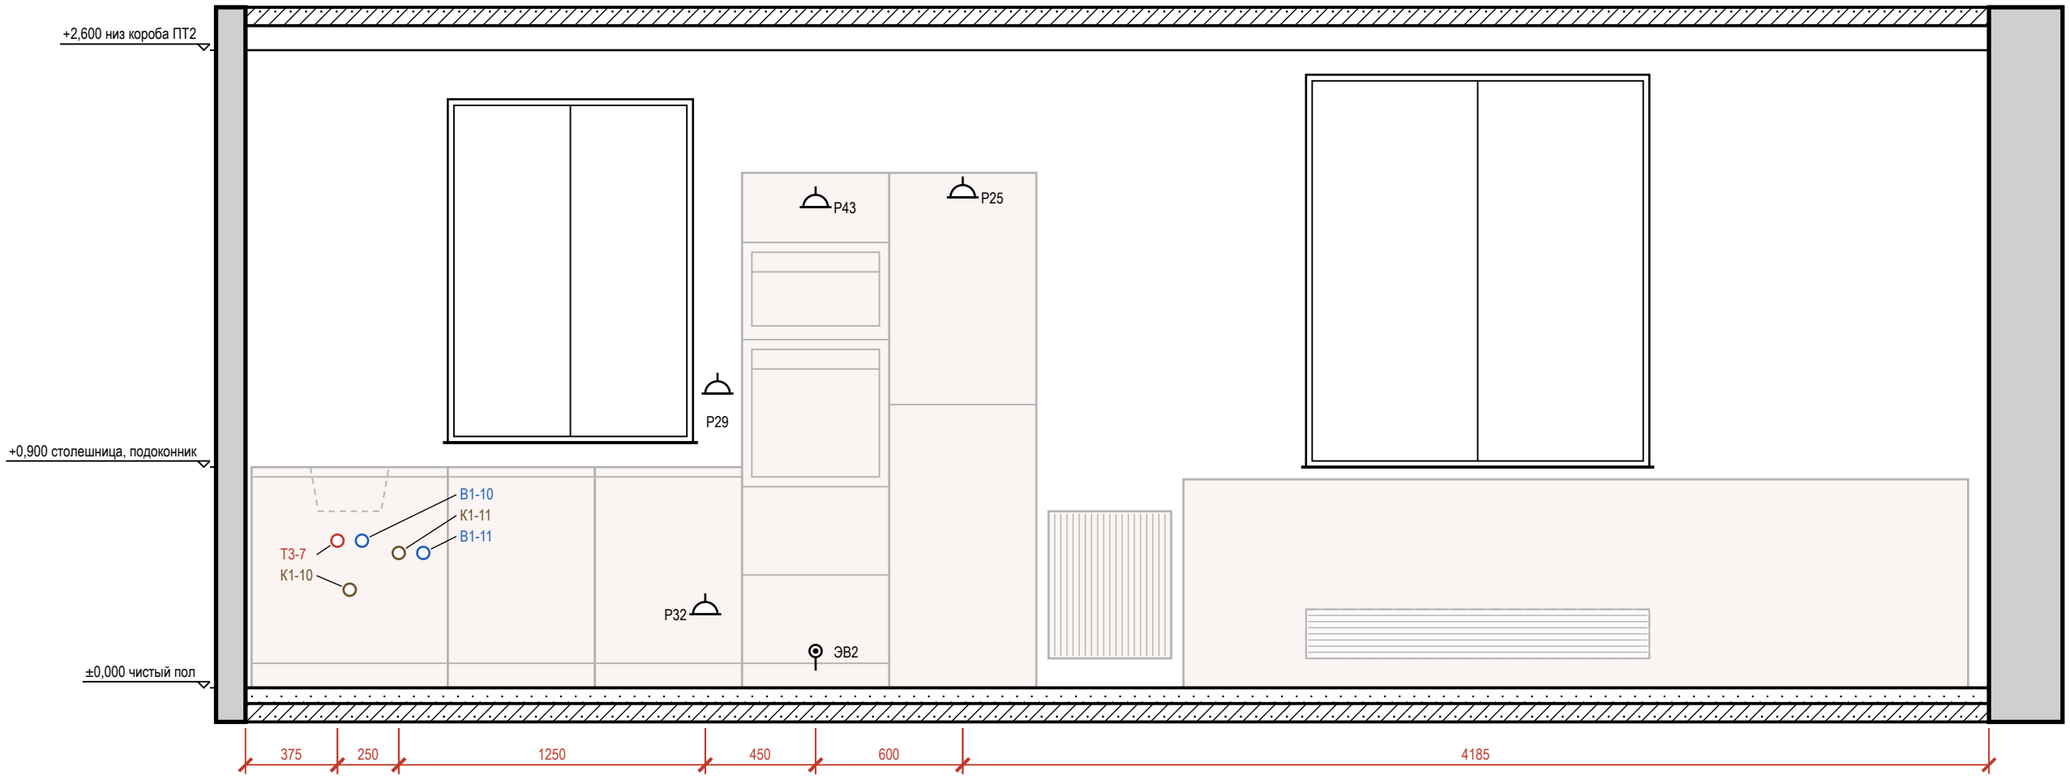



### Таблица привязок электроточек и выводов

| Марка | Назначение | От угла, мм | Н от пола, мм | Примечание |
|---|---|---|---|---|
| Т3-7 | горячая вода — мойка кухонная | 375 | 600 | межос. 100 |
| К1-10 | канализация — мойка кухонная | 425 | 400 | Ø50 |
| В1-10 | холодная вода — мойка кухонная | 475 | 600 | межос. 100 |
| К1-11 | канализация — посудомоечная машина | 625 | 550 | Ø40; слив ПММ в шкафу мойки |
| В1-11 | холодная вода — посудомоечная машина | 725 | 550 | кран ПММ в шкафу мойки |
| Р32 | розетка: посудомоечная машина — в соседнем модуле, за ящиком | 1875 | 300 | гр. 10 |
| Р29 | розетка: фартук | 1925 | 1200 | гр. 7 |
| ЭВ2 | вывод кабеля: духовой шкаф — в цоколе | 2325 | 150 | гр. 9 |
| Р43 | розетка: СВЧ — над нишей, съёмная панель | 2325 | 1960 | гр. 7 |
| Р25 | розетка: холодильник — над нишей, съёмная панель | 2925 | 2000 | гр. 11 |

### Условные обозначения

- розетка с заземляющим контактом; у знака — марка, ×N постов в рамке, гр. — группа щита, Н — высота оси, мм
- вывод кабеля для подключения прибора (без розетки), марка ЭВ
- вывод В1 (код — в ведомости привязок)
- вывод Т3 (код — в ведомости привязок)
- вывод К1 (код — в ведомости привязок)
- привязки точек и выводов от угла и от пола, мм
- марка развёртки: буква стены, стрелка — взгляд

### Схема развёрток (М 1:200)

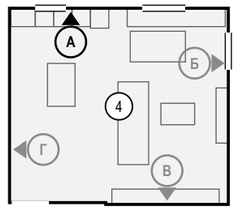



### Примечания


1. Вид «Привязки» стены А — электроточки и выводы ВК; архитектурная развёртка (мебель, отделка, проёмы, высоты) — на листе 88. Мебель и приборы — подложкой для ориентира; их марки и обозначения мебели, проёмов и стен — там же.
2. Привязки — в мм: по горизонтали от левого чистового угла стены до оси изделия, Н — от чистого пола до оси; все точки — в таблице привязок. Красная цепочка — привязки по осям; точки ближе 150 мм одна к другой в цепочку не дробятся — их привязки только в таблице.
3. У знака — марка электроточки (Р — розетка, S — выключатель, Св — светильник, ЭВ — вывод кабеля); условные обозначения и общие указания — лист 27.
4. Коды выводов ВК: В1 — холодная вода, Т3 — горячая вода, К1 — канализация; номер после дефиса — номер вывода на листе выводов сантехники.
5. Выводы кухонной техники — по утверждённому проекту кухни: привязки выводов даются от осей модулей гарнитура.

| | | | | | | |
|---|---|---|---|---|---|---|
| | | | | | Проект: Квартира с кабинетом | М 1:25 |
| | Лист | № док. | Подпись | Дата | Привязки электроточек и выводов ВК, стена А. Кухня-гостиная (пом. 4) | Стадия / Лист / Листов |
| Дизайнер | Кырлан А.С. | | | 04.11.26 | | П / 89 / 127 |

## Развёртка стены Б

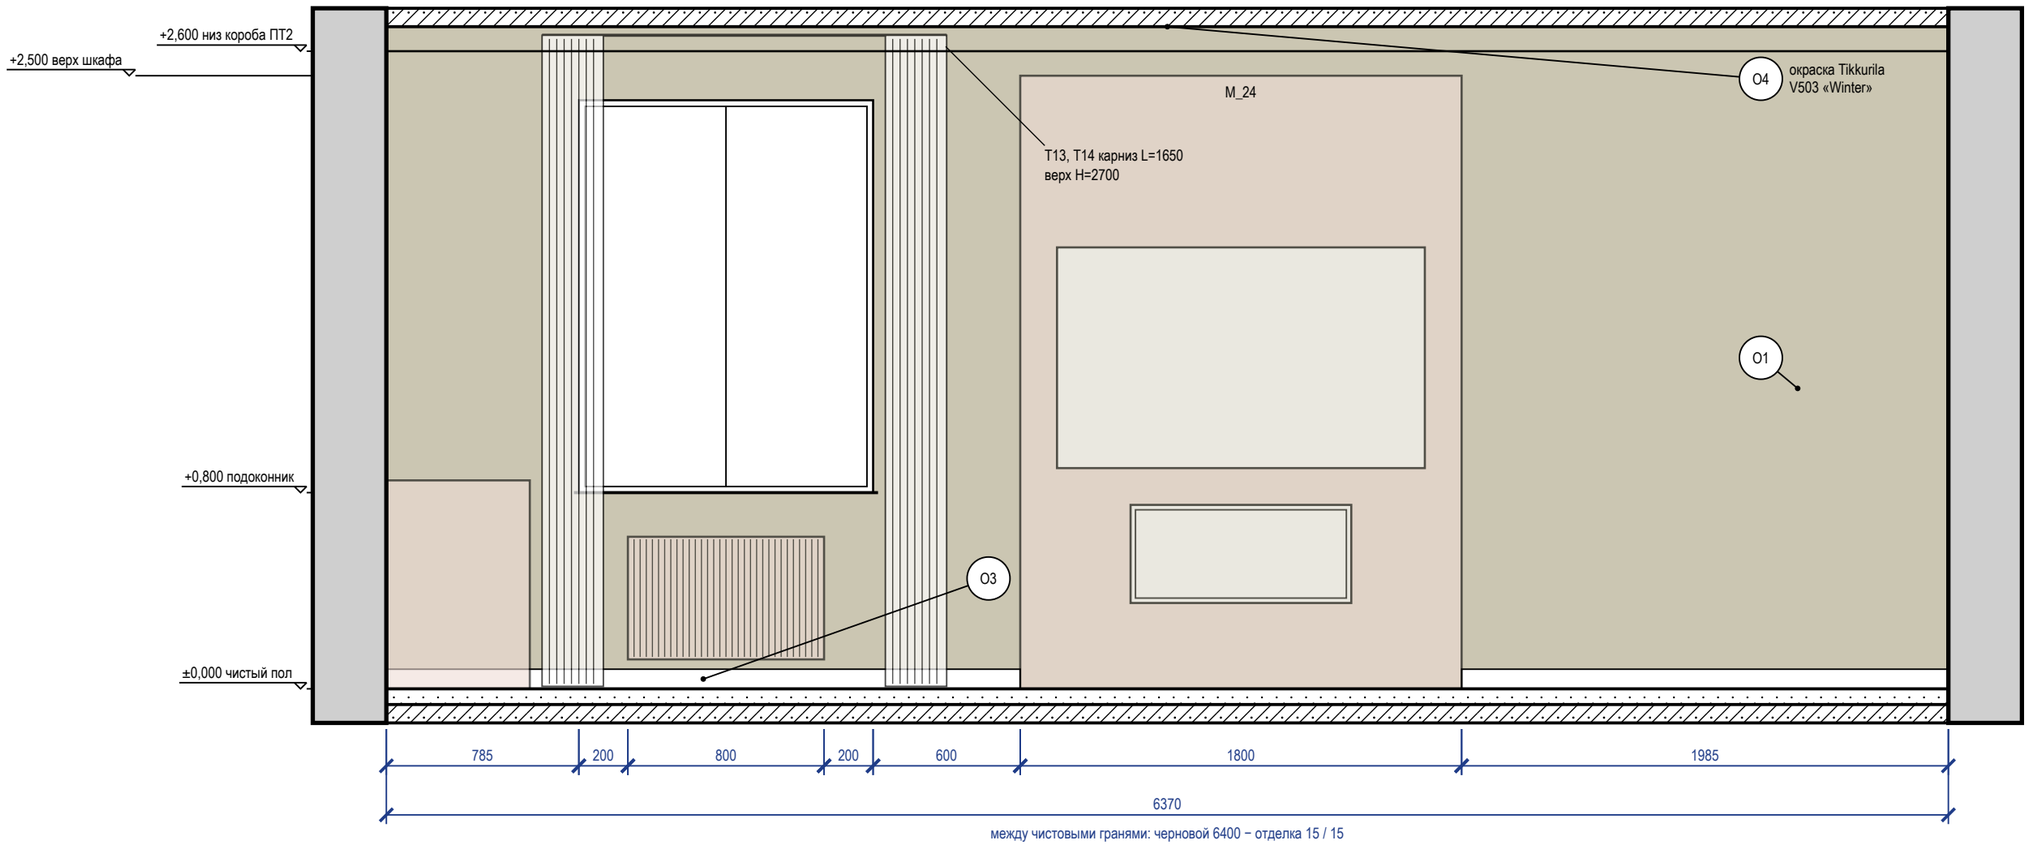



### Схема развёрток (М 1:100)

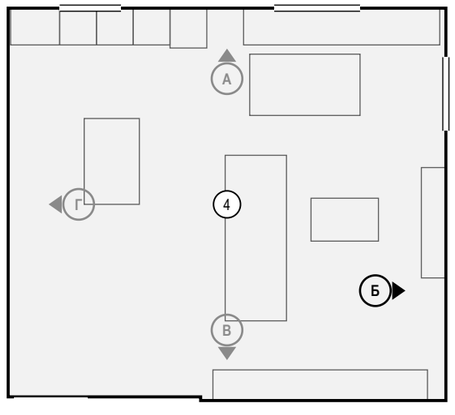


### Ведомость отделки (на листе)

| Марка | Поверхность | Материал, изделие | Цвет, код | Кол. |
|---|---|---|---|---|
| O1 | стены | окраска, Farrow & Ball Modern Emulsion, матовая, подготовка Q3 | Farrow & Ball No. 15 «Bone — мягкий каменно-серый с зеленцой» | 15,3 м² |
| O3 | плинтус | плинтус МДФ, h 80 мм, аналог: плинтус МДФ под покраску 80×16 | Farrow & Ball No. 15 «Bone — мягкий каменно-серый с зеленцой» | 4,6 м |
| O4 | потолок | окраска, Tikkurila Anti-Reflex 2, глубокоматовая, подготовка Q3 | Tikkurila V503 «Winter» | 45,5 м² |

Визуализация этой стены — лист 12

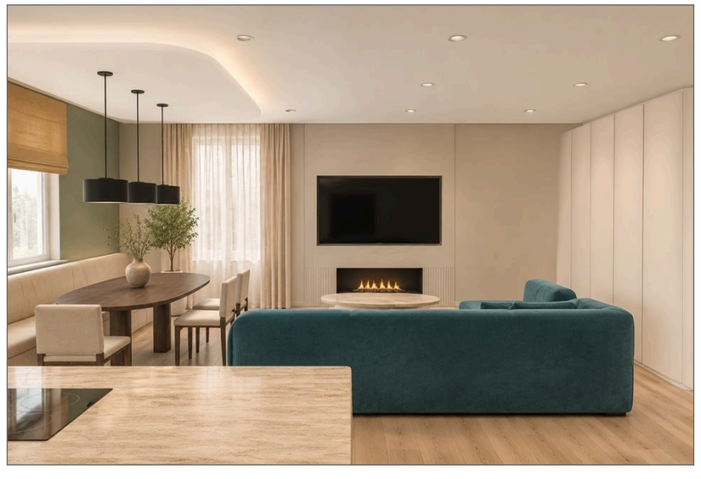


### Примечания

1. Размеры — в мм от чистовых поверхностей стен; условные обозначения и общие указания — лист 27.
2. Стена Б показана двумя видами: здесь — архитектурная развёртка (мебель, отделка, проёмы, высоты), электроточки и выводы ВК с привязками и таблицей — на листе 91 («Привязки»).
3. Карнизы (шины) — по ведомости текстиля декоратора: длина L и верх H на развёртке — те же числа, что в ведомости; крепление — до окраски потолка.
4. Потолок — у каждой стены свой, по плану потолков (НШ2, ПТ2); ступени — зоной, кромка короба перед нишей — тонкой линией; в поле потолка: ПТ1 +2,500.

| | | | | | | |
|---|---|---|---|---|---|---|
| | | | | | Проект: Квартира с кабинетом | М 1:25 |
| | Лист | № док. | Подпись | Дата | | |
| Дизайнер | Кырлан А.С. | | | 04.11.26 | Развёртка стены Б. Кухня-гостиная (пом. 4) | Стадия: П; Лист: 90; Листов: 127 |

## Развёртка стены Б: электроточки и выводы

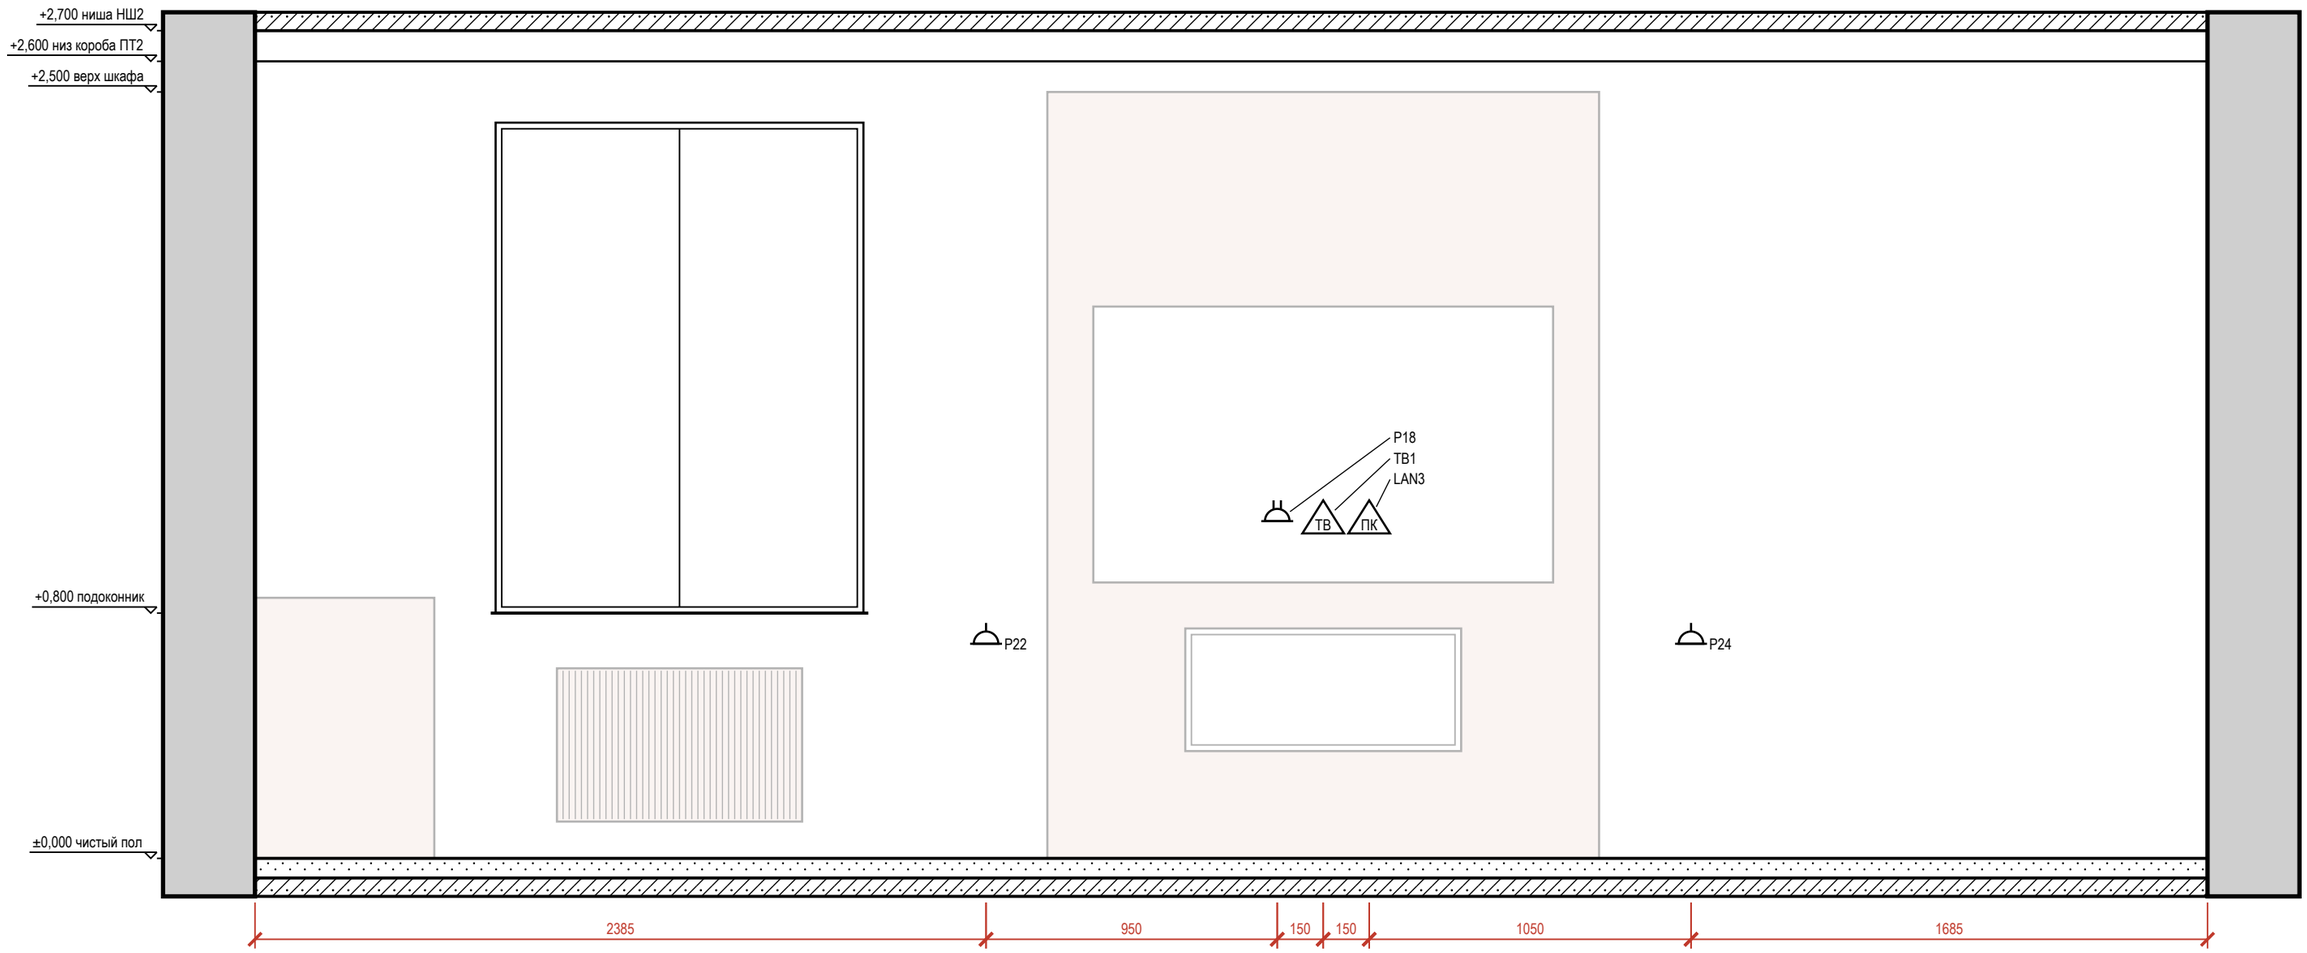



### Таблица привязок электроточек и выводов

| Марка | Назначение | От угла, мм | Н от пола, мм | Примечание |
|---|---|---|---|---|
| P22 | розетка: общего назначения | 2385 | 700 | гр. 6 |
| P18 | розетка: ТВ-зона: питание ТВ и приставки | 3335 | 1100 | рамка 2 поста, гр. 6 |
| TB1 | розетка ТВ: ТВ-зона | 3485 | 1100 | |
| LAN3 | розетка RJ45: ТВ-зона: Smart TV | 3635 | 1100 | |
| P24 | розетка: общего назначения | 4685 | 700 | гр. 6 |

### Условные обозначения

- розетка с заземляющим контактом; у знака — марка, ×N постов в рамке, гр. — группа щита, Н — высота оси, мм
- ПК — розетка компьютерная RJ45
- ТВ — розетка телевизионная
- привязки точек и выводов от угла и от пола, мм
- А — марка развёртки: буква стены, стрелка — взгляд

### Схема развёрток (М 1:200)

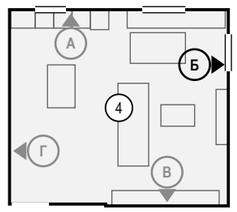



### Примечания

1. Вид «Привязки» стены Б — электроточки и выводы ВК; архитектурная развёртка (мебель, отделка, проёмы, высоты) — на листе 90. Мебель и приборы — подложкой для ориентира; их марки и обозначения мебели, проёмов и стен — там же.
2. Привязки — в мм: по горизонтали от левого чистового угла стены до оси изделия, Н — от чистого пола до оси; все точки — в таблице привязок. Красная цепочка — привязки по осям; точки ближе 120 мм одна к другой в цепочку не дробятся — их привязки только в таблице.
3. У знака — марка электроточки (Р — розетка, S — выключатель, Св — светильник, ЭВ — вывод кабеля); условные обозначения и общие указания — лист 27.


| | | | | | |
|---|---|---|---|---|---|
| | | | | | Проект: Квартира с кабинетом — М 1:20 |
| | Лист | № док. | Подпись | Дата | |
| Дизайнер | Кырлан А.С. | | | 04.11.26 | Привязки электроточек, стена Б. Кухня-гостиная (пом. 4) |
| | | | | | Стадия: П; Лист: 91; Листов: 127 |

выпуск 04.11.2026 № 627e1ac6ce · стр. 91 из 127

## Развёртка стены В

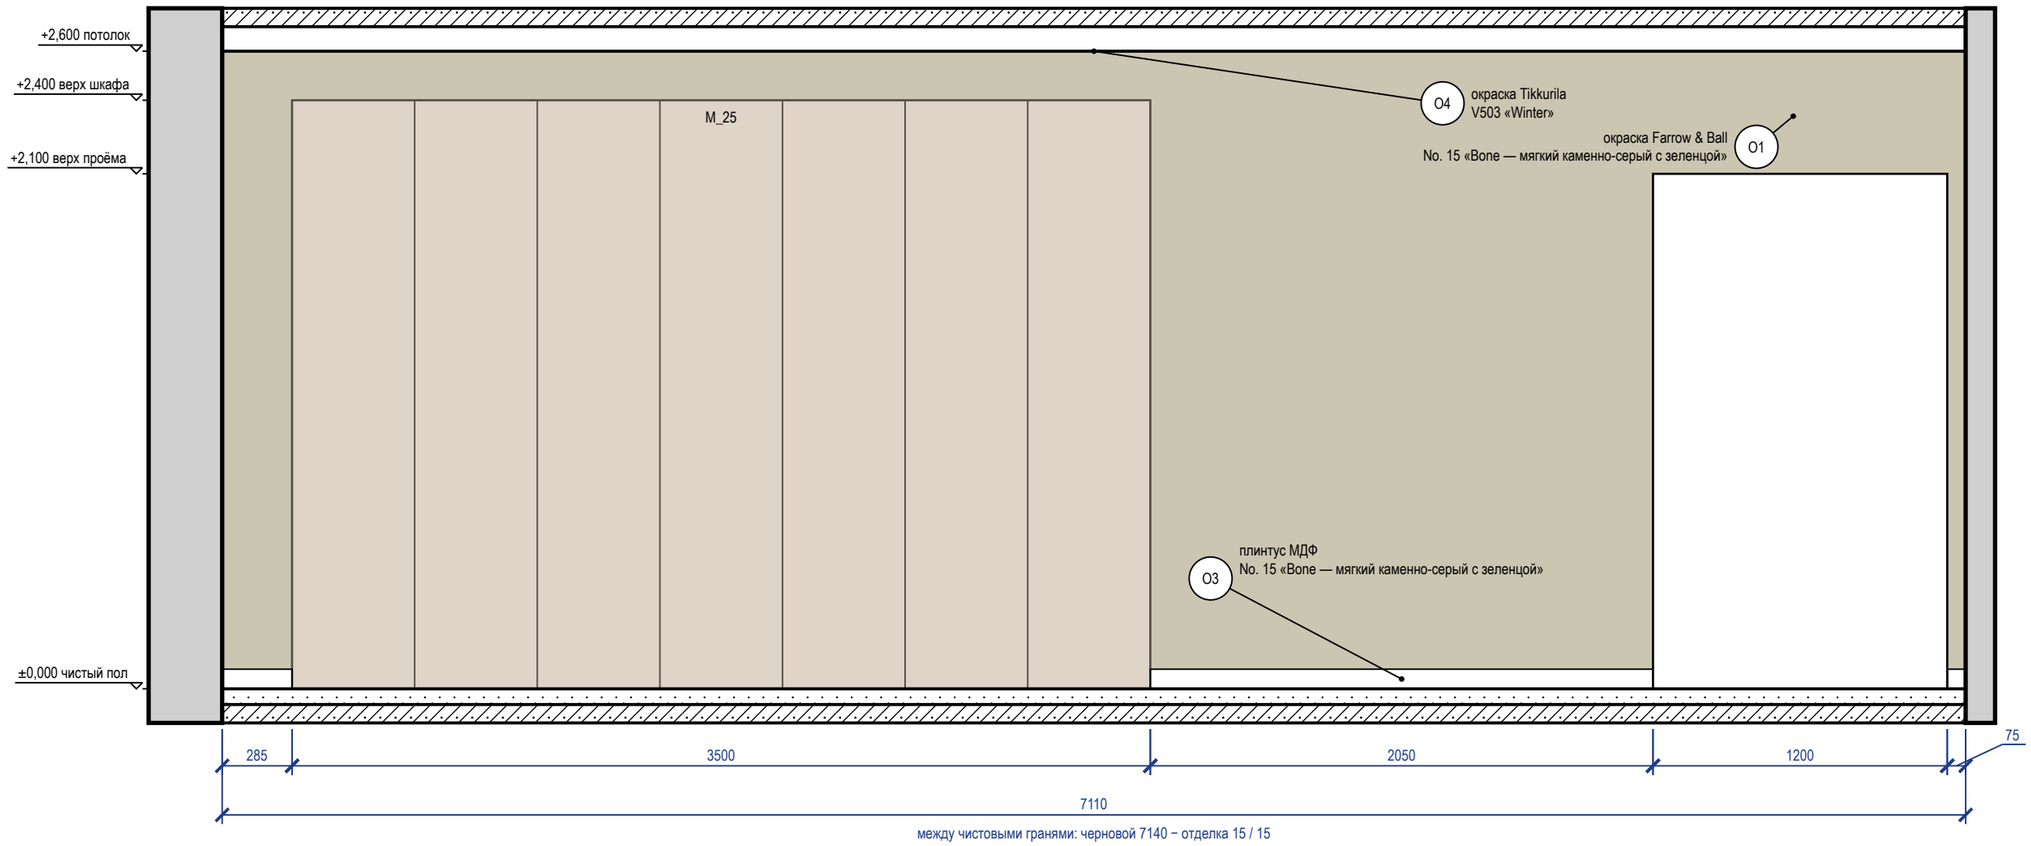



### Схема развёрток (М 1:100)

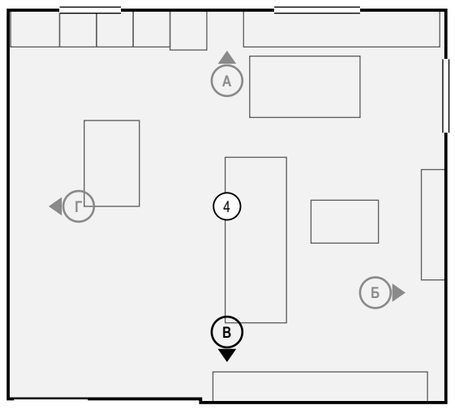


### Ведомость отделки (на листе)

| Марка | Поверхность | Материал, изделие | Цвет, код | Кол. |
|---|---|---|---|---|
| O1 | стены | окраска, Farrow & Ball Modern Emulsion, матовая, подготовка Q3 | Farrow & Ball No. 15 «Bone — мягкий каменно-серый с зеленцой» | 16 м² |
| O3 | плинтус | плинтус МДФ, h 80 мм, аналог: плинтус МДФ под покраску 80×16 | Farrow & Ball No. 15 «Bone — мягкий каменно-серый с зеленцой» | 2,4 м |
| O4 | потолок | окраска, Tikkurila Anti-Reflex 2, глубокоматовая, подготовка Q3 | Tikkurila V503 «Winter» | 45,5 м² |

Визуализация этой стены — лист 13

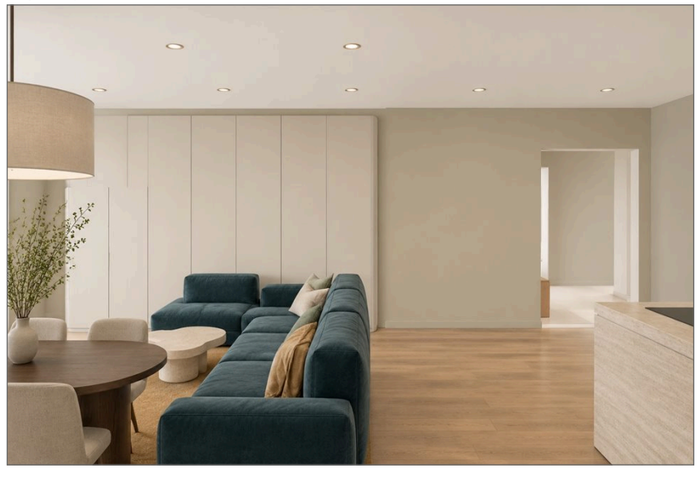


### Примечания

1. Размеры — в мм от чистовых поверхностей стен; условные обозначения и общие указания — лист 27.
2. Потолок — у каждой стены свой, по плану потолков (ПТ2); ступени — зоной, кромка короба перед нишей — тонкой линией; в поле потолка: ПТ1 +2,500.


| | | | | | | |
|---|---|---|---|---|---|---|
| | | | | | Проект: Квартира с кабинетом | М 1:25 |
| | Лист | № док. | Подпись | Дата | Развёртка стены В. Кухня-гостиная (пом. 4) | Стадия / Лист / Листов |
| Дизайнер | Кырлан А.С. | | | 04.11.26 | | П / 92 / 127 |

## Развёртка стены А1

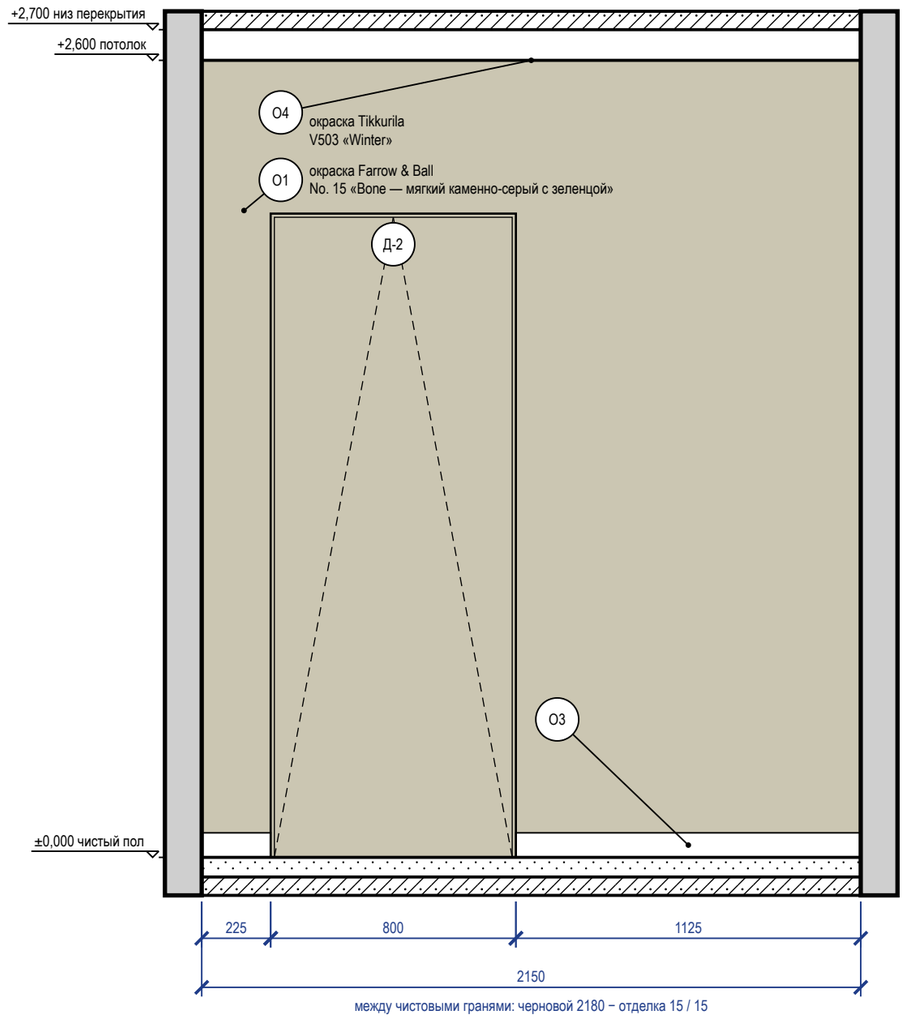



между чистовыми гранями: черновой 2180 − отделка 15 / 15

## Развёртка стены Г

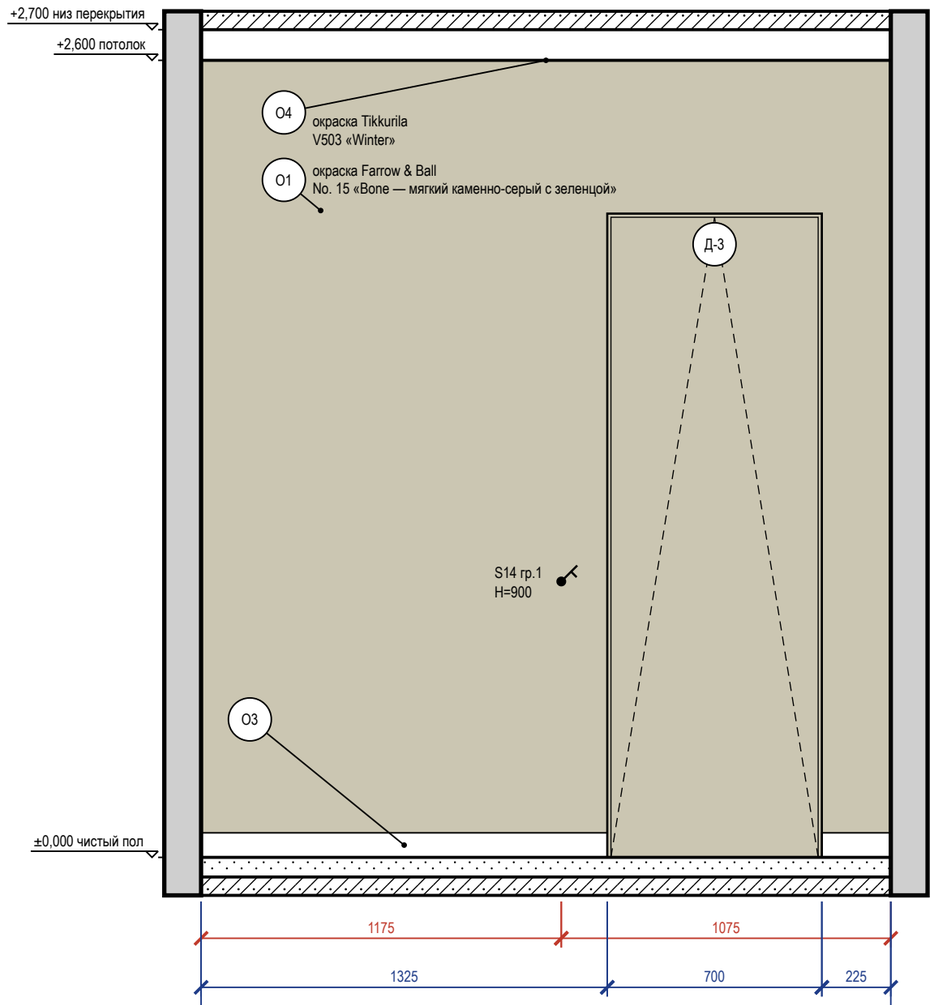


между чистовыми гранями: черновой 2280 − отделка 15 / 15

### Схема развёрток (М 1:100)

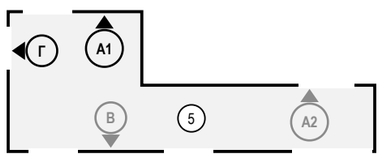


### Ведомость отделки (на листе)

| Марка | Поверхность | Материал, изделие | Цвет, код | Кол. |
|---|---|---|---|---|
| О1 | стены | окраска, Farrow & Ball Modern Emulsion, матовая, подготовка Q3 | Farrow & Ball No. 15 «Bone — мягкий каменно-серый с зеленцой» | 8,3 м² |
| О3 | плинтус | плинтус МДФ, h 80 мм, аналог: плинтус МДФ под покраску 80×16 | Farrow & Ball No. 15 «Bone — мягкий каменно-серый с зеленцой» | 2,9 м |
| О4 | потолок | окраска, Tikkurila Anti-Reflex 2, глубокоматовая, подготовка Q3 | Tikkurila V503 «Winter» | 9,1 м² |

### Примечания

1. Размеры — в мм от чистовых поверхностей стен; условные обозначения и общие указания — лист 27.
2. Двери скрытого монтажа — полотно в плоскости стены, отделка стены по полотну, плинтус прерывается у короба (узел — на листе узлов).


| | | | | |
|---|---|---|---|---|
| | Лист | № док. | Подпись | Дата |
| Дизайнер | Кырлан А.С. | | | 04.11.26 |

Проект: Квартира с кабинетом — М 1:20


Развёртки стен А1, Г. Коридор (пом. 5)

| Стадия | Лист | Листов |
|---|---|---|
| П | 93 | 127 |

## Развёртка стены А2

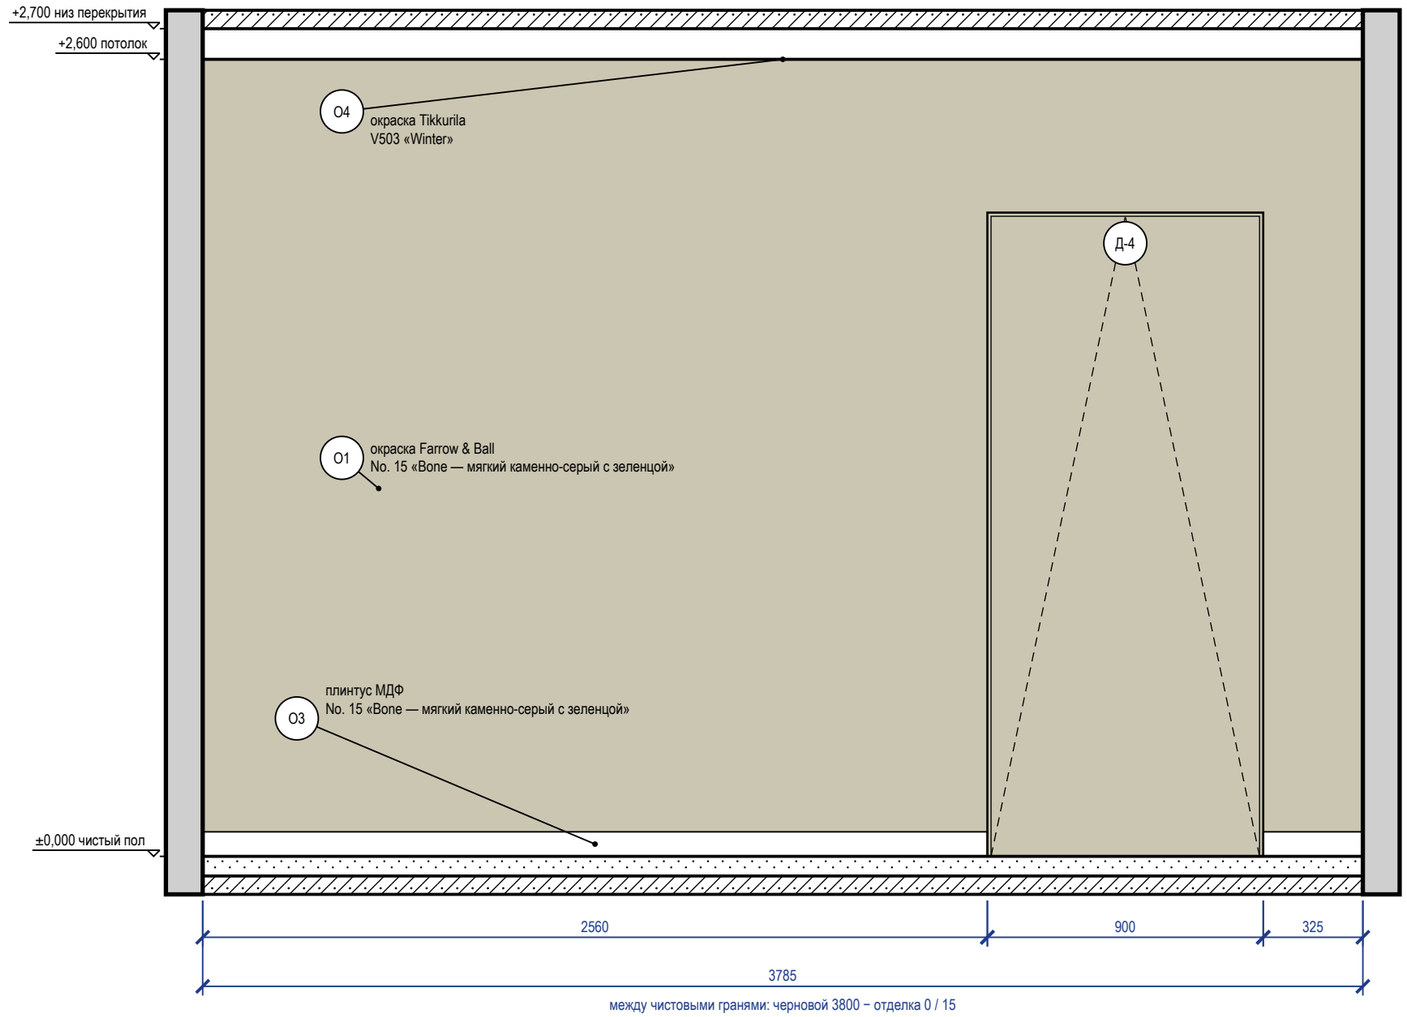


### Схема развёрток (М 1:100)

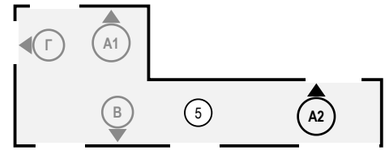


### Ведомость отделки (на листе)

| Марка | Поверхность | Материал, изделие | Цвет, код | Кол. |
|---|---|---|---|---|
| О1 | стены | окраска, Farrow & Ball Modern Emulsion, матовая, подготовка Q3 | Farrow & Ball No. 15 «Bone — мягкий каменно-серый с зеленцой» | 8 м² |
| О3 | плинтус | плинтус МДФ, h 80 мм, аналог: плинтус МДФ под покраску 80×16 | Farrow & Ball No. 15 «Bone — мягкий каменно-серый с зеленцой» | 2,9 м |
| О4 | потолок | окраска, Tikkurila Anti-Reflex 2, глубокоматовая, подготовка Q3 | Tikkurila V503 «Winter» | 9,1 м² |


### Примечания

1. Размеры — в мм от чистовых поверхностей стен; условные обозначения и общие указания — лист 27.
2. Двери скрытого монтажа — полотно в плоскости стены, отделка стены по полотну, плинтус прерывается у короба (узел — на листе узлов).


| | | | | | |
|---|---|---|---|---|---|
| | | | | | Проект: Квартира с кабинетом — М 1:20 |
| | Лист | № док. | Подпись | Дата | Развёртка стены А2. Коридор (пом. 5) |
| Дизайнер | Кырлан А.С. | | | 04.11.26 | Стадия: П · Лист: 94 · Листов: 127 |

выпуск 04.11.2026 № 627e1ac6ce · стр. 94 из 127

## Развёртка стены В

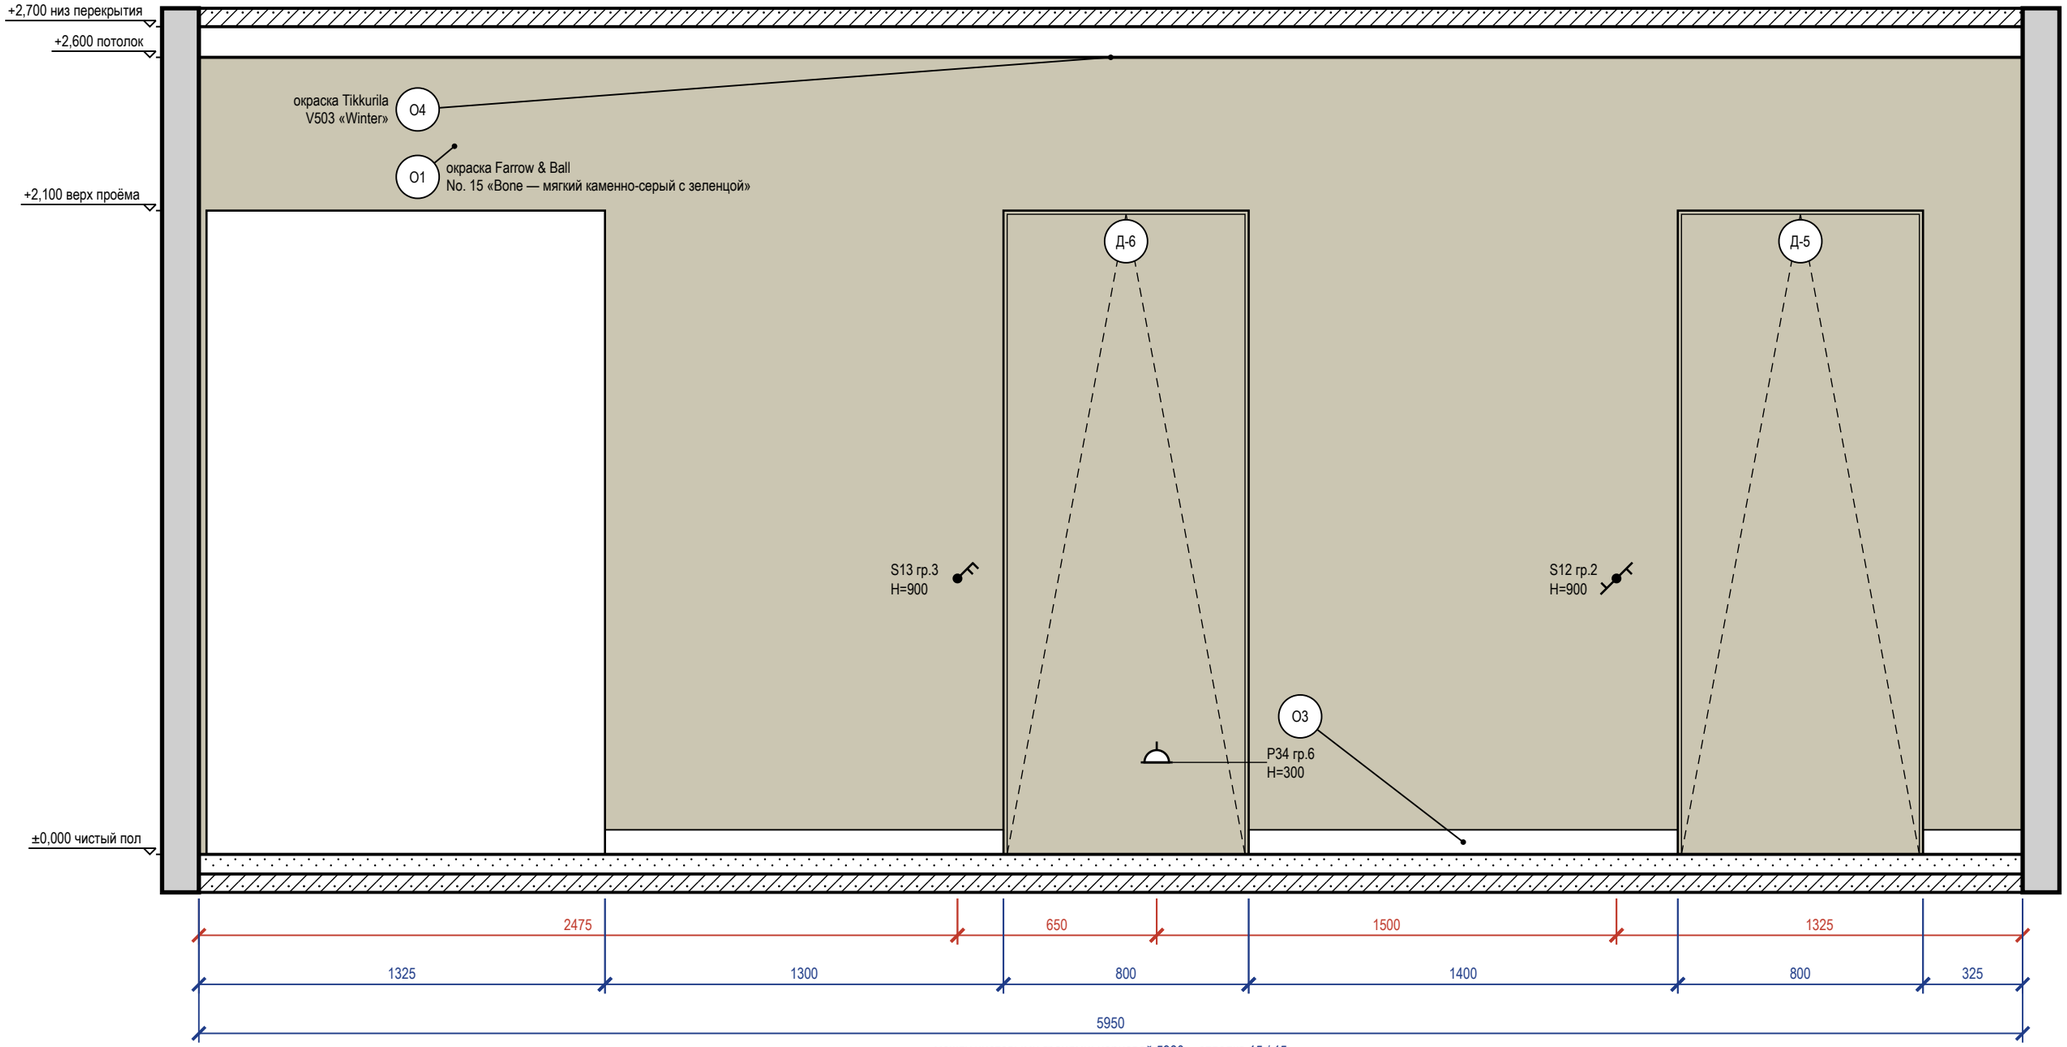



### Схема развёрток (М 1:100)

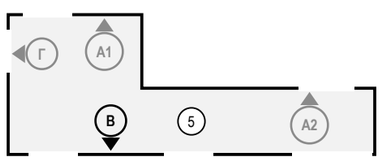


### Ведомость отделки (на листе)

| Марка | Поверхность | Материал, изделие | Цвет, код | Кол. |
|---|---|---|---|---|
| О1 | стены | окраска, Farrow & Ball Modern Emulsion, матовая, подготовка Q3 | Farrow & Ball No. 15 «Bone — мягкий каменно-серый с зеленцой» | 9,4 м² |
| О3 | плинтус | плинтус МДФ, h 80 мм, аналог: плинтус МДФ под покраску 80×16 | Farrow & Ball No. 15 «Bone — мягкий каменно-серый с зеленцой» | 3 м |
| О4 | потолок | окраска, Tikkurila Anti-Reflex 2, глубокоматовая, подготовка Q3 | Tikkurila V503 «Winter» | 9,1 м² |

Визуализация этой стены — лист 15

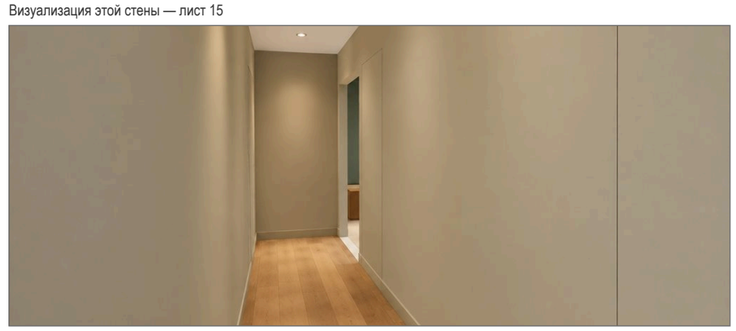

### Примечания

1. Размеры — в мм от чистовых поверхностей стен; условные обозначения и общие указания — лист 27.
2. Двери скрытого монтажа — полотно в плоскости стены, отделка стены по полотну, плинтус прерывается у короба (узел — на листе узлов).


| | | | | |
|---|---|---|---|---|
| | Лист | № док. | Подпись | Дата |
| Дизайнер | Кырлан А.С. | | | 04.11.26 |

Проект: Квартира с кабинетом — М 1:20

Развёртка стены В. Коридор (пом. 5)


| Стадия | Лист | Листов |
|---|---|---|
| П | 95 | 127 |

## Развёртка стены А

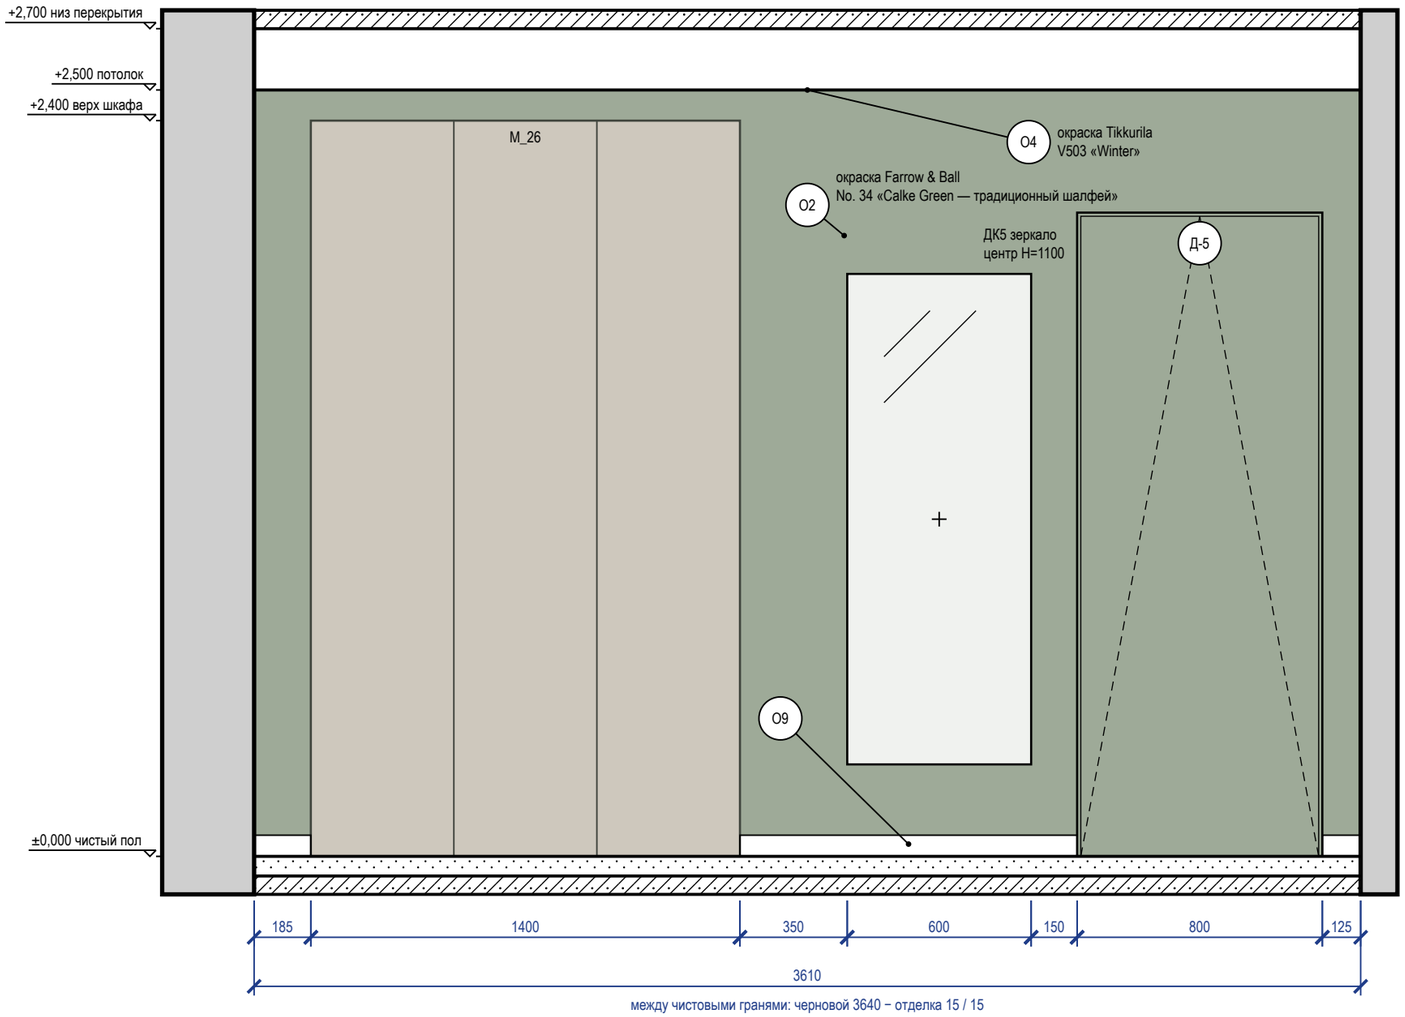


между чистовыми гранями: черновой 3640 − отделка 15 / 15

### Схема развёрток (М 1:100)

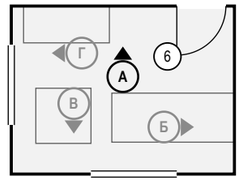


### Ведомость отделки (на листе)

| Марка | Поверхность | Материал, изделие | Цвет, код | Кол. |
|---|---|---|---|---|
| О2 | акцентная стена | окраска, Farrow & Ball Modern Emulsion, матовая, подготовка Q3 | Farrow & Ball No. 34 «Calke Green традиционный шалфей» | 7,3 м² |
| О4 | потолок | окраска, Tikkurila Anti-Reflex 2, глубокоматовая, подготовка Q3 | Tikkurila V503 «Winter» | 10 м² |
| О9 | плинтус | плинтус МДФ, Orac Decor Contour (Luxxus), h 69 мм, SX165 | Farrow & Ball No. 15 «Bone — мягкий каменно-серый с зеленцой» | 1,4 м |

Визуализация этой стены — лист 16




### Примечания


1. Размеры — в мм от чистовых поверхностей стен; условные обозначения и общие указания — лист 27.
2. Картины и зеркала крепить к основанию по паспорту изделия (закладные и анкеры — в перечне скрытых работ); крест — ось центра предмета.
3. Двери скрытого монтажа — полотно в плоскости стены, отделка стены по полотну, плинтус прерывается у короба (узел — на листе узлов).
4. Потолок — у каждой стены свой, по плану потолков (ПТ1); ступени — зоной, кромка короба перед нишей — тонкой линией; в поле потолка: ПТ2 +2,600.

| | | | | | | |
|---|---|---|---|---|---|---|
| | | | | | Проект: Квартира с кабинетом | М 1:20 |
| | Лист | № док. | Подпись | Дата | Развёртка стены А. Детская (пом. 6) | Стадия / Лист / Листов |
| Дизайнер | Кырлан А.С. | | | 04.11.26 | | П / 96 / 127 |

## Развёртка стены Б

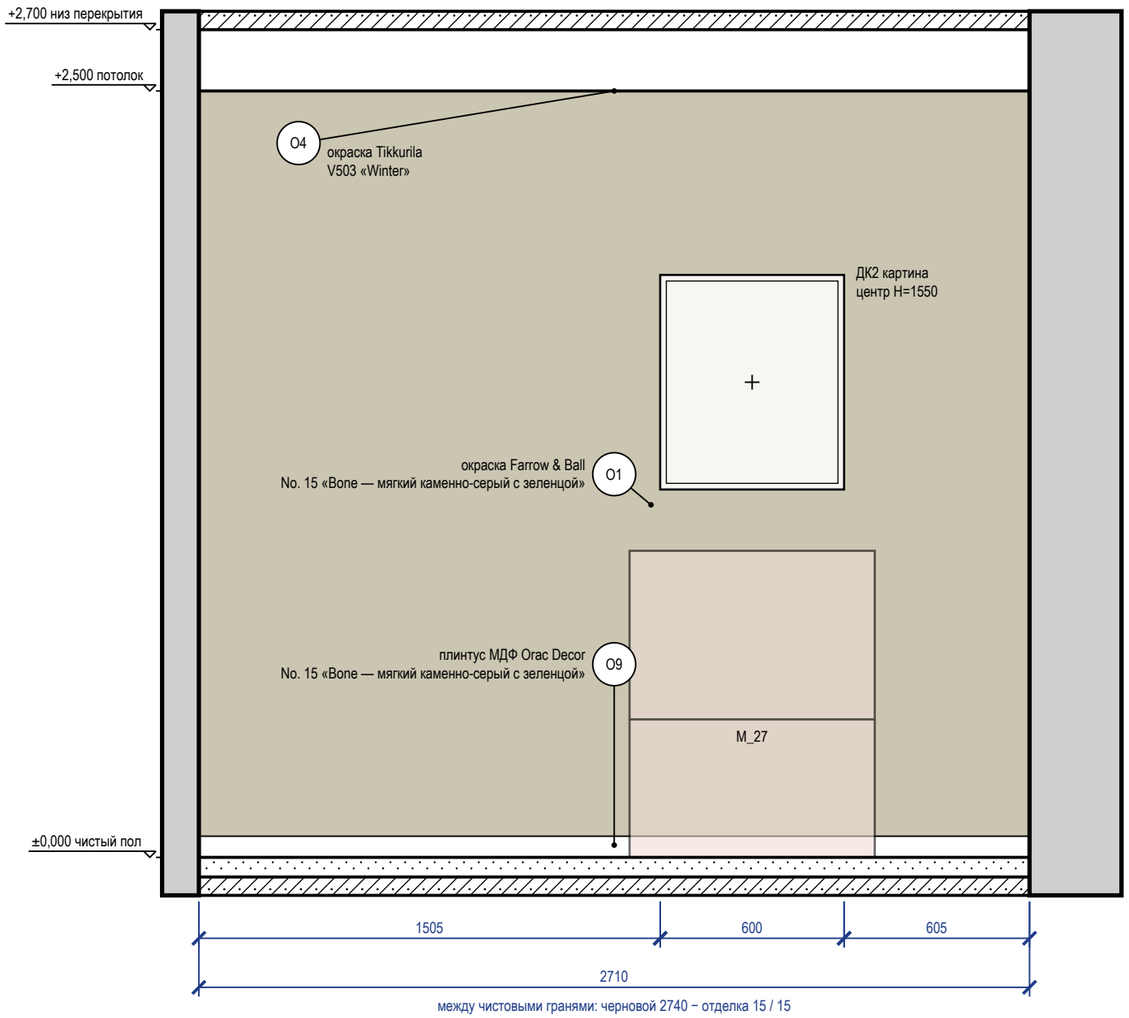



### Схема развёрток (М 1:100)

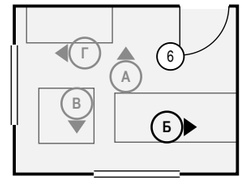


### Ведомость отделки (на листе)

| Марка | Поверхность | Материал, изделие | Цвет, код | Кол. |
|---|---|---|---|---|
| О1 | стены | окраска, Farrow & Ball Modern Emulsion, матовая, подготовка Q3 | Farrow & Ball No. 15 «Bone — мягкий каменно-серый с зеленцой» | 6,8 м² |
| О4 | потолок | окраска, Tikkurila Anti-Reflex 2, глубокоматовая, подготовка Q3 | Tikkurila V503 «Winter» | 10 м² |
| О9 | плинтус | плинтус МДФ, Orac Decor Contour (Luxxus), h 69 мм, SX165 | Farrow & Ball No. 15 «Bone — мягкий каменно-серый с зеленцой» | 2,7 м |

Визуализация этой стены — лист 17

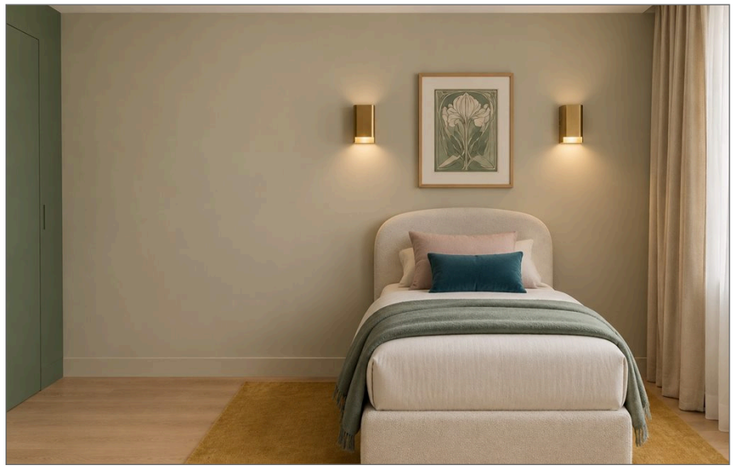


### Примечания

1. Размеры — в мм от чистовых поверхностей стен; условные обозначения и общие указания — лист 27.
2. Стена Б показана двумя видами: здесь — архитектурная развёртка (мебель, отделка, проёмы, высоты), электроточки и выводы ВК с привязками и таблицей — на листе 98 («Привязки»).
3. Картины и зеркала крепить к основанию по паспорту изделия (закладные и анкеры — в перечне скрытых работ); крест — ось центра предмета.
4. Потолок — у каждой стены свой, по плану потолков (ПТ1); ступени — зоной, кромка короба перед нишей — тонкой линией; в поле потолка: ПТ2 +2,600.

| | | | | | | |
|---|---|---|---|---|---|---|
| | | | | | Проект: Квартира с кабинетом | М 1:20 |
| | Лист | № док. | Подпись | Дата | | |
| Дизайнер | Кырлан А.С. | | | 04.11.26 | Развёртка стены Б. Детская (пом. 6) | Стадия: П; Лист: 97; Листов: 127 |

## Развёртка стены Б: электроточки и выводы

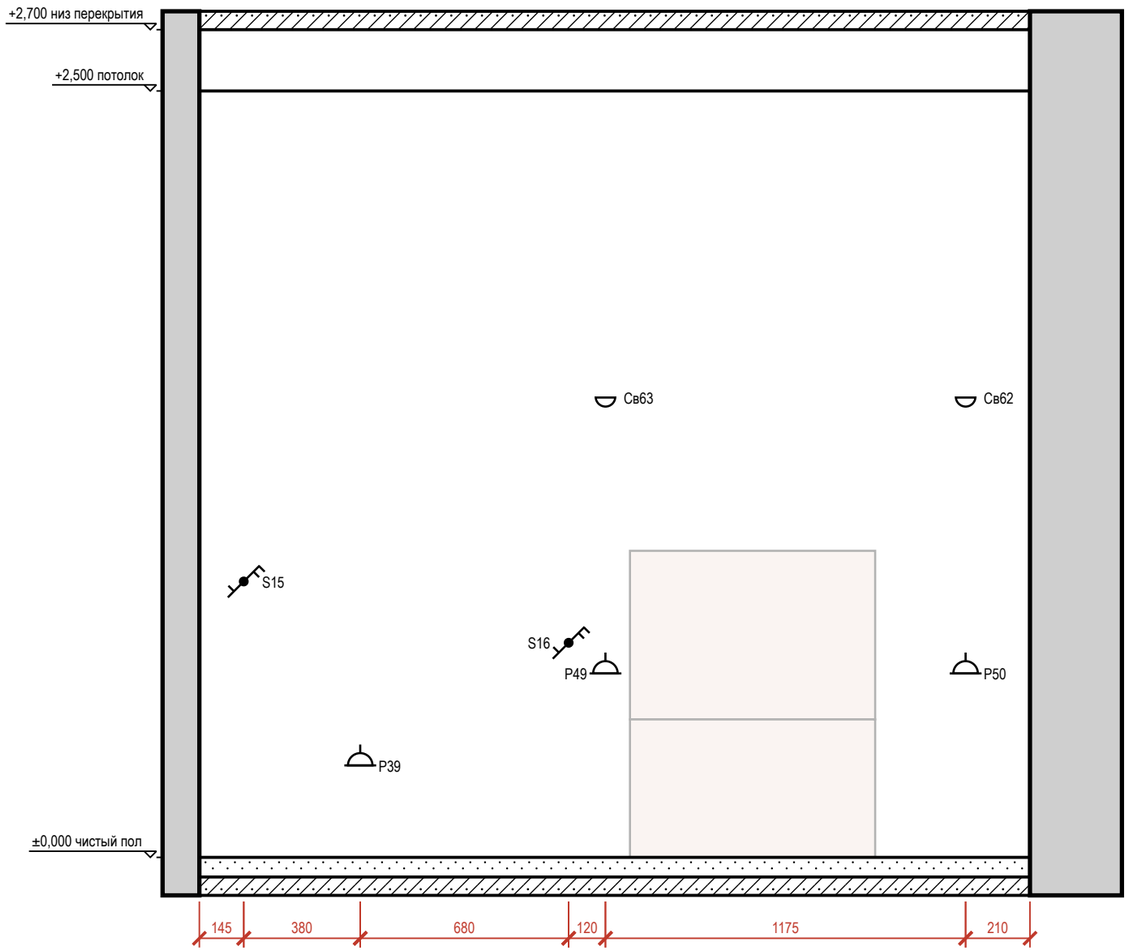



## Таблица привязок электроточек и выводов

| Марка | Назначение | От угла, мм | Н от пола, мм | Примечание |
|---|---|---|---|---|
| S15 | выключатель | 145 | 900 | гр. 1 |
| P39 | розетка: уборка | 525 | 300 | гр. 5 |
| S16 | выключатель | 1205 | 700 | гр. 1 |
| P49 | розетка: у кровати | 1325 | 600 | гр. 5 |
| Св63 | светильник настенный | 1325 | 1500 | гр. 1 |
| P50 | розетка: у кровати | 2500 | 600 | гр. 5 |
| Св62 | светильник настенный | 2500 | 1500 | гр. 1 |

## Условные обозначения

- розетка с заземляющим контактом; у знака — марка, ×N постов в рамке, гр. — группа щита, Н — высота оси, мм
- выключатель одноклавишный
- выключатель двухклавишный (флажков — по числу клавиш)
- выключатель с проходной или перекрёстной клавишей (обратный флажок); тип клавиши — в подписи
- светильник настенный (бра), Н — высота оси
- привязки точек и выводов от угла и от пола, мм
- марка развёртки: буква стены, стрелка — взгляд

## Схема развёрток (М 1:50)

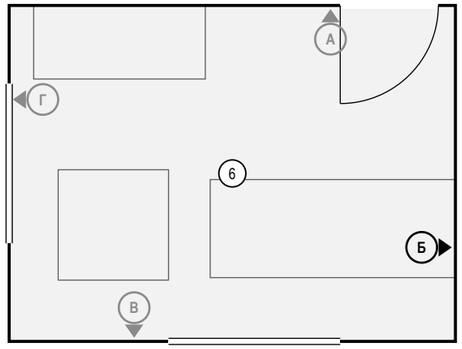



## Примечания


1. Вид «Привязки» стены Б — электроточки и выводы ВК; архитектурная развёртка (мебель, отделка, проёмы, высоты) — на листе 97. Мебель и приборы — подложкой для ориентира; их марки и обозначения мебели, проёмов и стен — там же.
2. Привязки — в мм: по горизонтали от левого чистового угла стены до оси изделия, Н — от чистого пола до оси; все точки — в таблице привязок. Красная цепочка — привязки по осям; точки ближе 120 мм одна к другой в цепочку не дробятся — их привязки только в таблице.
3. У знака — марка электроточки (Р — розетка, S — выключатель, Св — светильник, ЭВ — вывод кабеля); условные обозначения и общие указания — лист 27.

| | | | | | |
|---|---|---|---|---|---|
| | | | | | Проект: Квартира с кабинетом — **М 1:20** |
| | Лист | № док. | Подпись | Дата | Привязки электроточек, стена Б. Детская (пом. 6) |
| Дизайнер | Кырлан А.С. | | | 04.11.26 | Стадия: П · Лист: 98 · Листов: 127 |

## Развёртка стены В

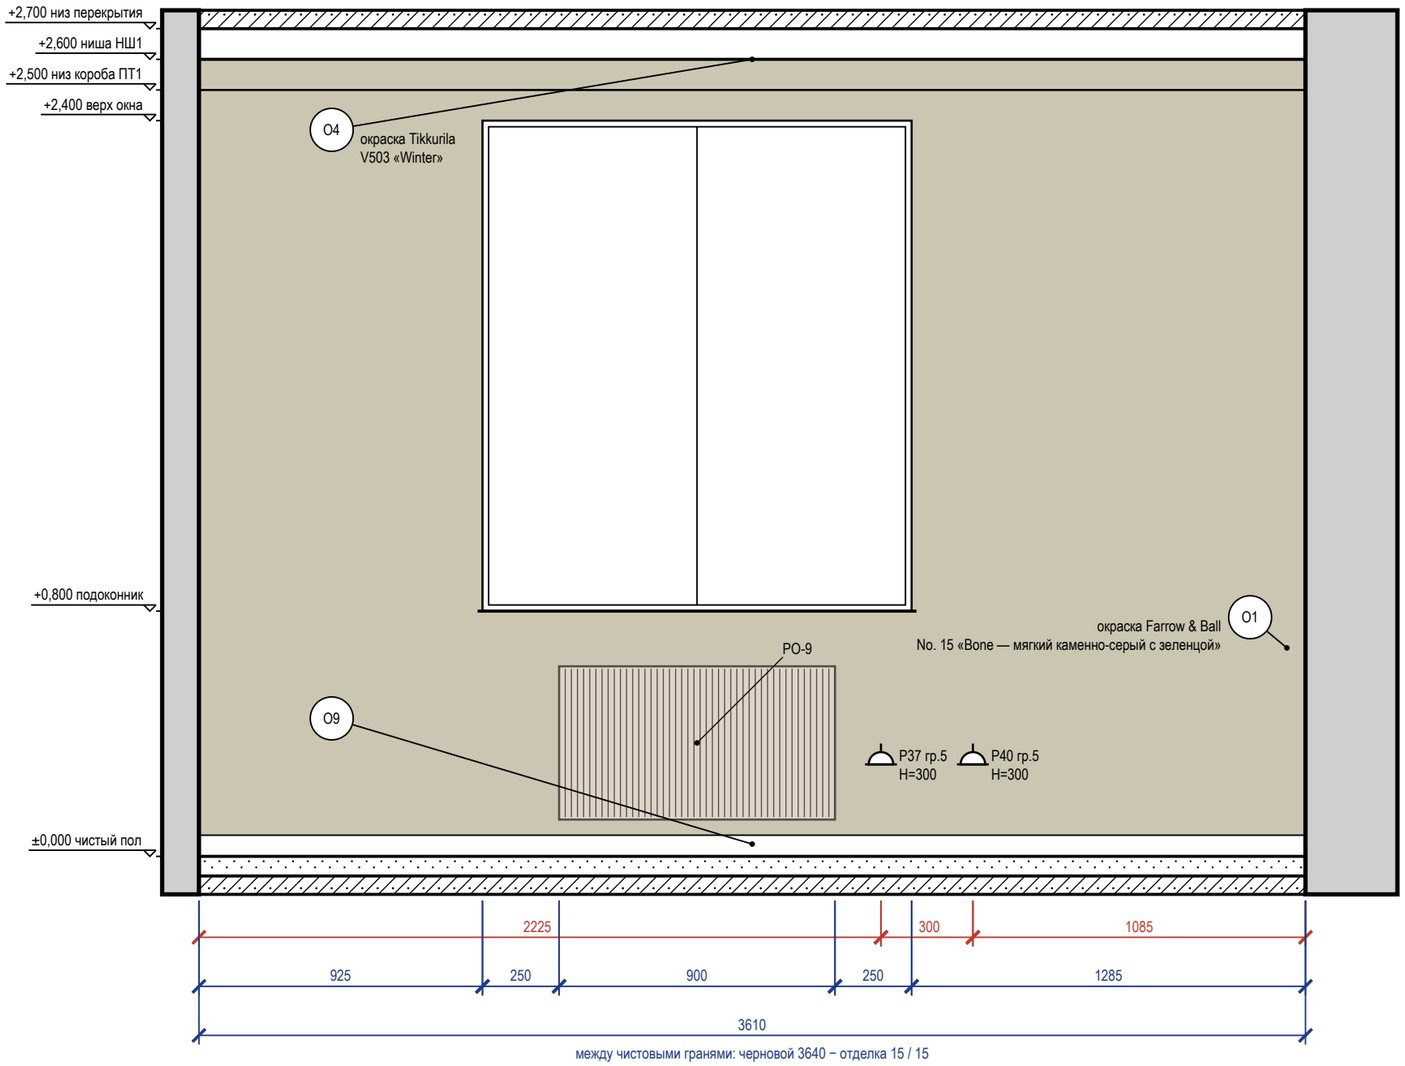


### Схема развёрток (М 1:100)

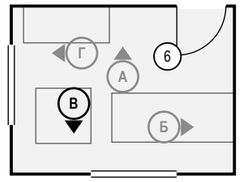


### Ведомость отделки (на листе)


| Марка | Поверхность | Материал, изделие | Цвет, код | Кол. |
|---|---|---|---|---|
| О1 | стены | окраска, Farrow & Ball Modern Emulsion, матовая, подготовка Q3 | Farrow & Ball No. 15 «Bone — мягкий каменно-серый с зеленцой» | 7,1 м² |
| О4 | потолок | окраска, Tikkurila Anti-Reflex 2, глубокоматовая, подготовка Q3 | Tikkurila V503 «Winter» | 10 м² |
| О9 | плинтус | плинтус МДФ, Orac Decor Contour (Luxxus), h 69 мм, SX165 | Farrow & Ball No. 15 «Bone — мягкий каменно-серый с зеленцой» | 3,6 м |

### Примечания


1. Размеры — в мм от чистовых поверхностей стен; условные обозначения и общие указания — лист 27.
2. Потолок — у каждой стены свой, по плану потолков (НШ1, ПТ1); ступени — зоной, кромка короба перед нишей — тонкой линией; в поле потолка: ПТ2 +2,600.

| | | | | | |
|---|---|---|---|---|---|
| | | | | | Проект: Квартира с кабинетом — М 1:20 |
| | Лист | № док. | Подпись | Дата | Развёртка стены В. Детская (пом. 6) |
| Дизайнер | Кырлан А.С. | | | 04.11.26 | Стадия: П; Лист: 99; Листов: 127 |

## Развёртка стены Г

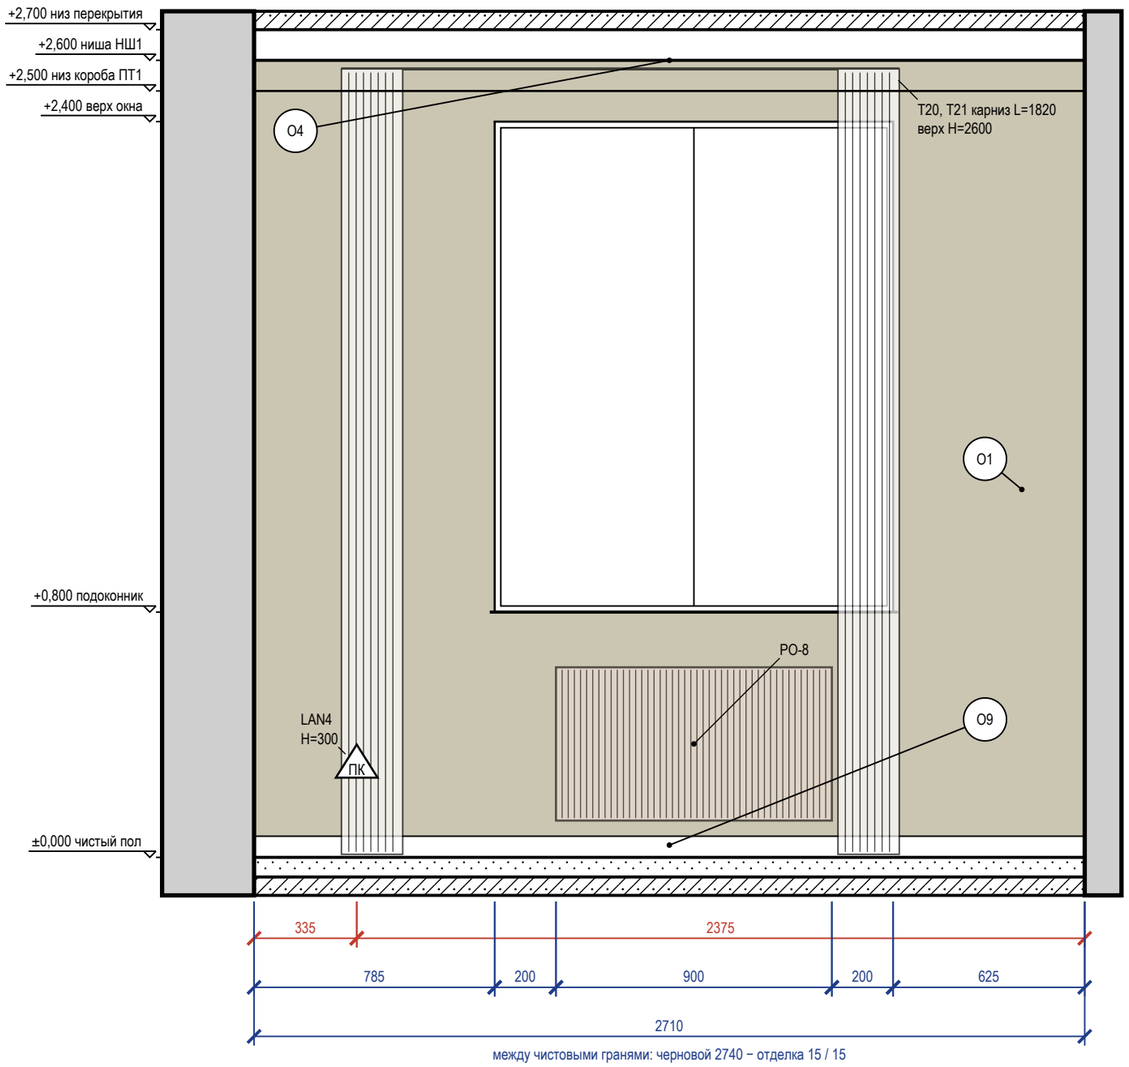


### Схема развёрток (М 1:100)

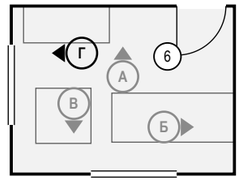


### Ведомость отделки (на листе)

| Марка | Поверхность | Материал, изделие | Цвет, код | Кол. |
|---|---|---|---|---|
| О1 | стены | окраска, Farrow & Ball Modern Emulsion, матовая, подготовка Q3 | Farrow & Ball No. 15 «Bone — мягкий каменно-серый с зеленцой» | 5 м² |
| О4 | потолок | окраска, Tikkurila Anti-Reflex 2, глубокоматовая, подготовка Q3 | Tikkurila V503 «Winter» | 10 м² |
| О9 | плинтус | плинтус МДФ, Orac Decor Contour (Luxxus), h 69 мм, SX165 | Farrow & Ball No. 15 «Bone — мягкий каменно-серый с зеленцой» | 2,7 м |

Визуализация этой стены — лист 18




### Примечания

1. Размеры — в мм от чистовых поверхностей стен; условные обозначения и общие указания — лист 27.
2. Карнизы (шины) — по ведомости текстиля декоратора: длина L и верх H на развёртке — те же числа, что в ведомости; крепление — до окраски потолка.
3. Потолок — у каждой стены свой, по плану потолков (НШ1, ПТ1); ступени — зоной, кромка короба перед нишей — тонкой линией; в поле потолка: ПТ2 +2,600.


| | | | | | | |
|---|---|---|---|---|---|---|
| | | | | | Проект: Квартира с кабинетом | М 1:20 |
| | Лист | № док. | Подпись | Дата | | |
| Дизайнер | Кырлан А.С. | | | 04.11.26 | Развёртка стены Г. Детская (пом. 6) | Стадия: П; Лист: 100; Листов: 127 |

## Развёртка стены А

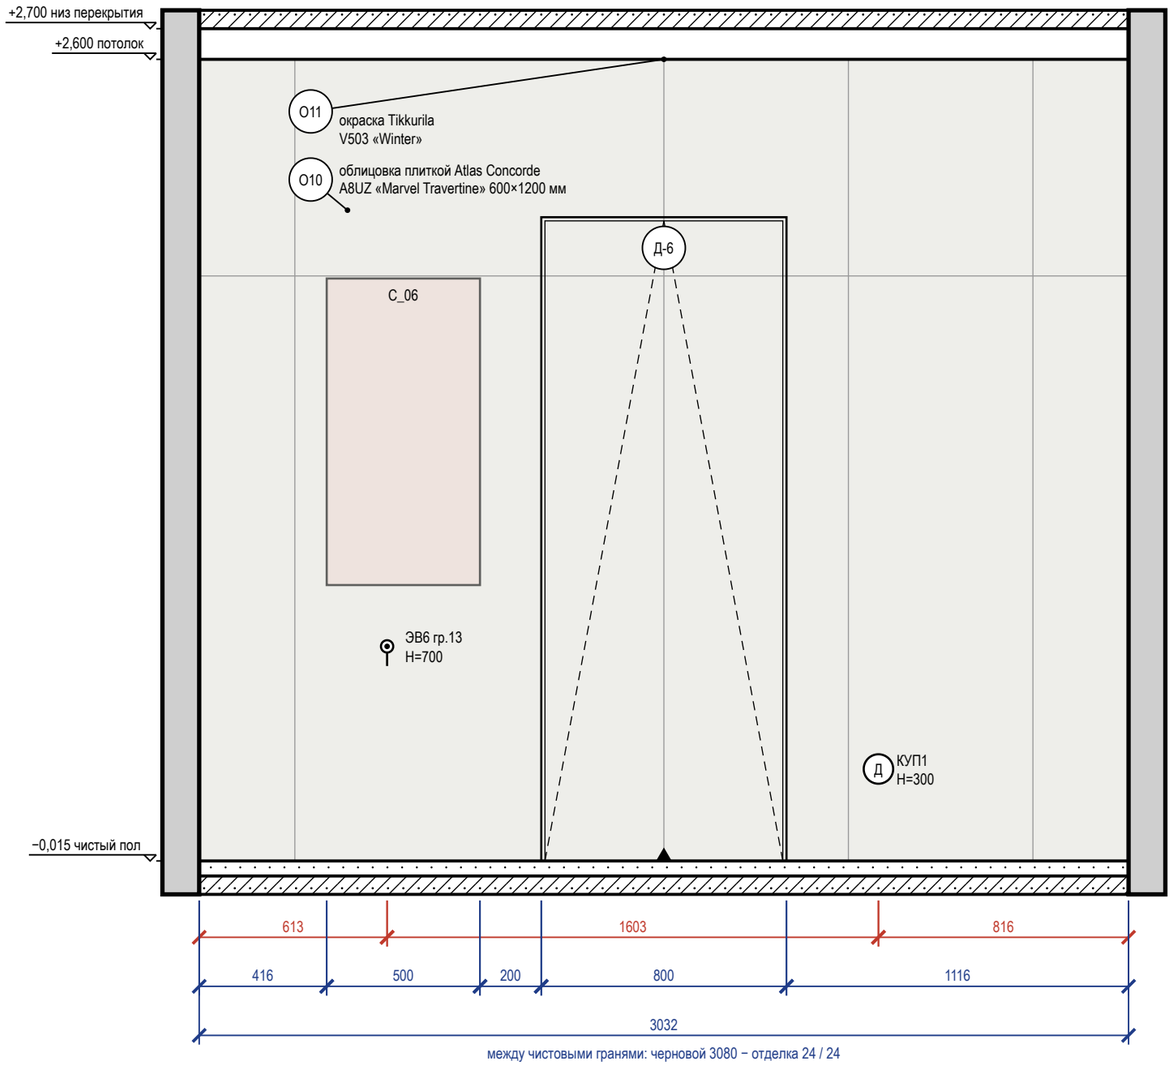



между чистовыми гранями: черновой 3080 − отделка 24 / 24

## Развёртка стены Б

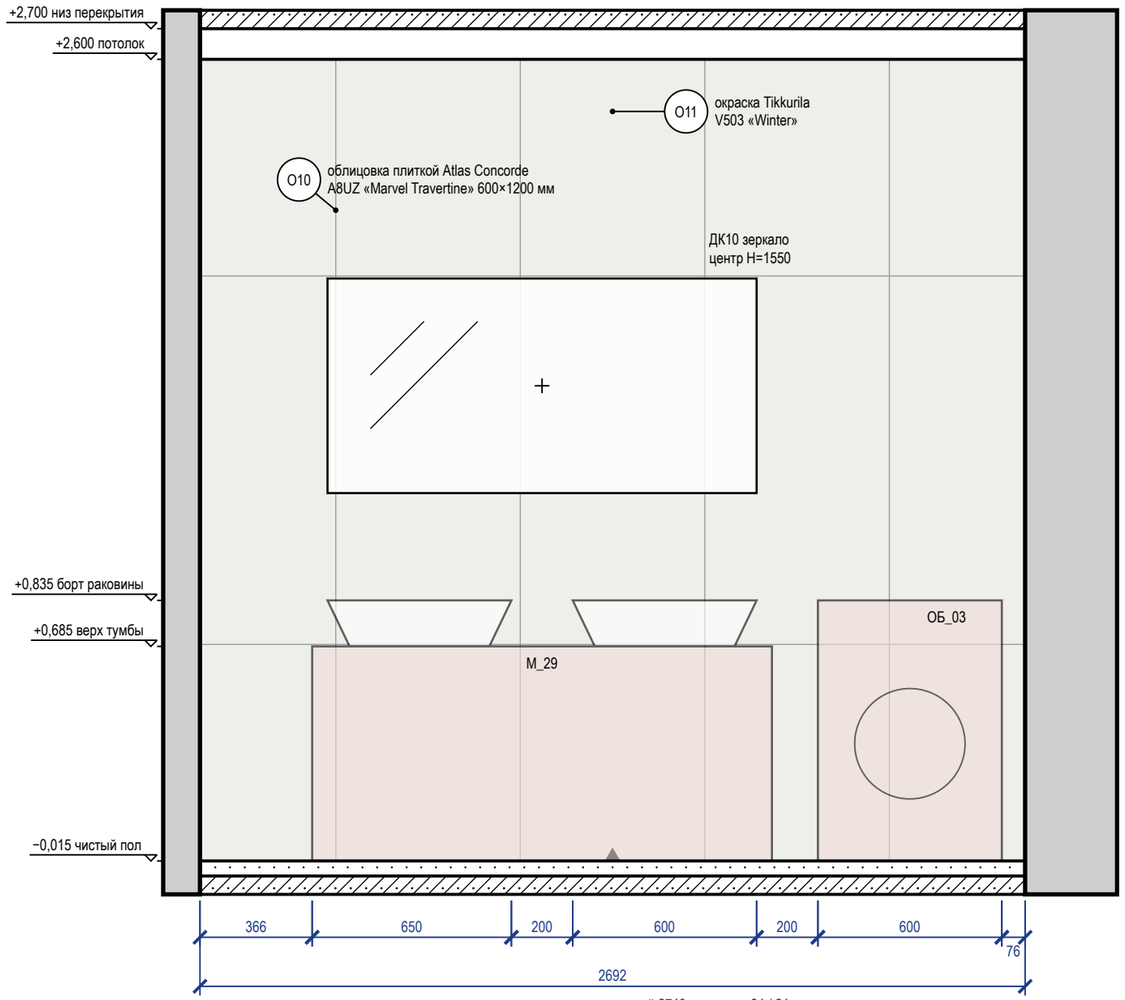


между чистовыми гранями: черновой 2740 − отделка 24 / 24

### Схема развёрток (М 1:100)

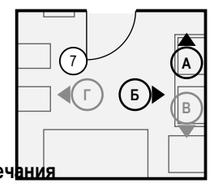


### Ведомость отделки (на листе)

| Марка | Поверхность | Материал, изделие | Цвет, код | Кол. |
|---|---|---|---|---|
| О10 | стены | облицовка плиткой, Atlas Concorde Marvel Travertine, 600×1200×9 мм, A8UZ, затирка CG2WA | Atlas Concorde A8UZ «Marvel Travertine» | 13,3 м² |
| О11 | потолок | окраска, Tikkurila Luja 7, матовая, подготовка Q3 | Tikkurila V503 «Winter» | 8,4 м² |

Визуализация этой стены — лист 19




### Примечания

1. Размеры — в мм от чистовых поверхностей стен; условные обозначения и общие указания — лист 27.
2. Стена Б показана двумя видами: здесь — архитектурная развёртка (мебель, отделка, проёмы, высоты), электроточки и выводы ВК с привязками и таблицей — на листе 103 («Привязки»).
3. Схема мебели, приборов и декора не является технической документацией для производства мебели; габариты — по паспортам изделий.
4. Облицовка — по сетке швов 2 мм, раскладка от оси стены (треугольник у пола), по высоте — от середины облицовки, подрезки у пола и у потолка поровну; подрезки — по листу раскладки плитки.
5. Гидроизоляция в 2 слоя, заход на стены 200 мм; над ванной — до 2000 и 300 мм за борт — до облицовки, с актом скрытых работ и тестом проливом (узел — на листе узлов).
6. Картины и зеркала крепить к основанию по паспорту изделия (закладные и анкеры — в перечне скрытых работ); крест — ось центра предмета.
7. Двери скрытого монтажа — полотно в плоскости стены, отделка стены по полотну, плинтус прерывается у короба (узел — на листе узлов).


| | | | | | | |
|---|---|---|---|---|---|---|
| | | | | | Проект: Квартира с кабинетом | М 1:20 |
| | Лист | № док. | Подпись | Дата | Развёртки стен А, Б. Ванная (пом. 7) | Стадия: П; Лист: 101; Листов: 127 |
| Дизайнер | Кырлан А.С. | | | 04.11.26 | | |

## Развёртка стены В

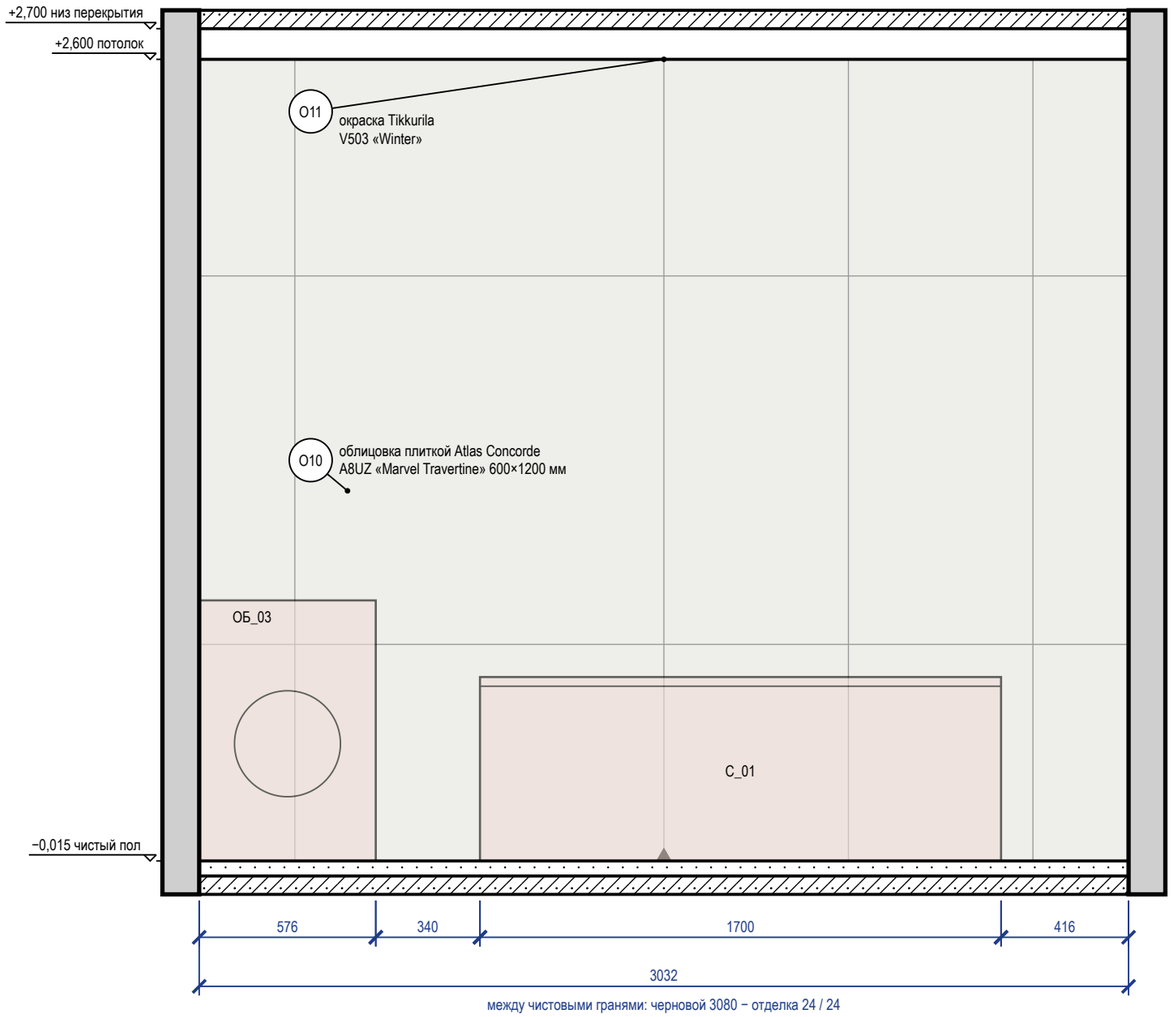



между чистовыми гранями: черновой 3080 − отделка 24 / 24

## Развёртка стены Г

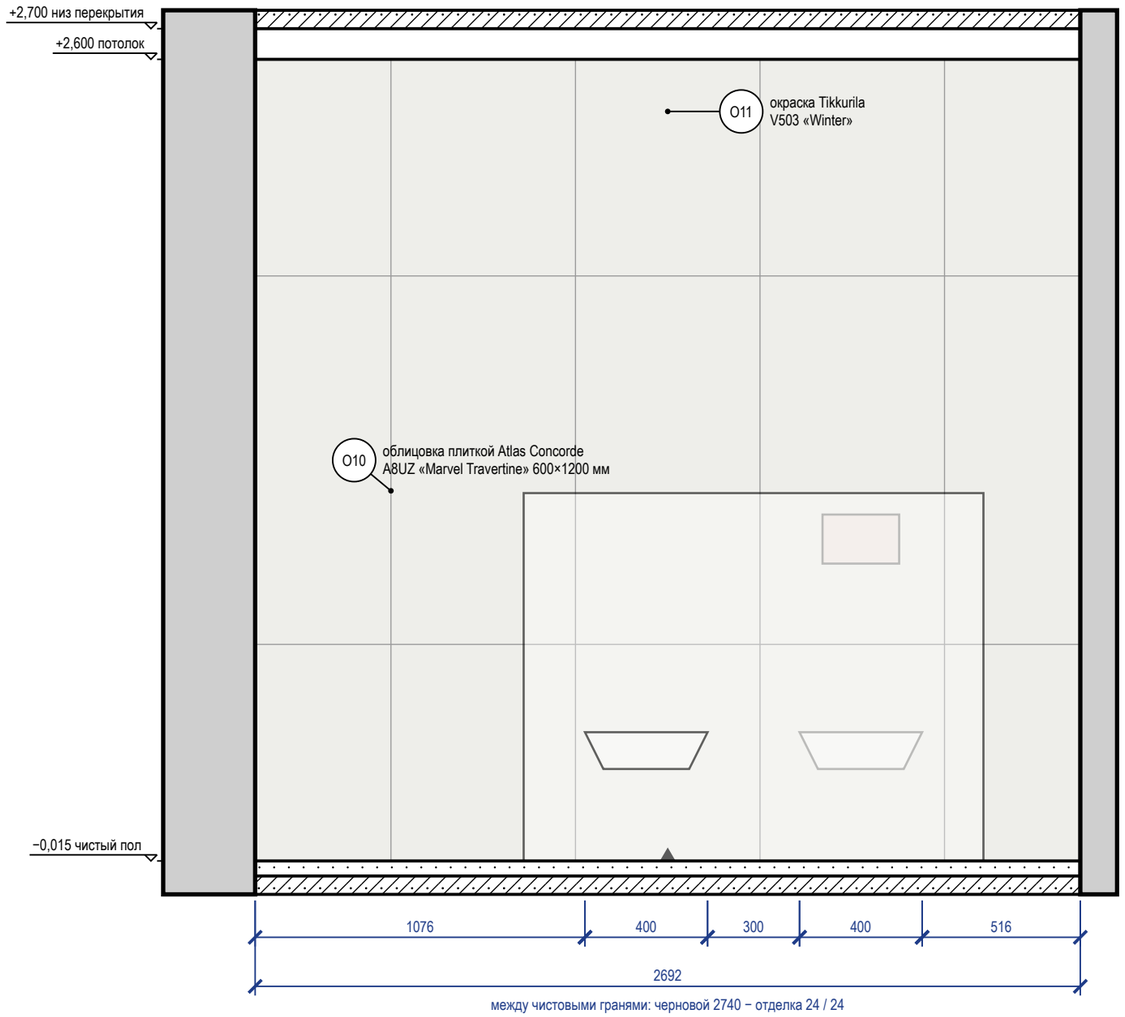


между чистовыми гранями: черновой 2740 − отделка 24 / 24

### Схема развёрток (М 1:100)

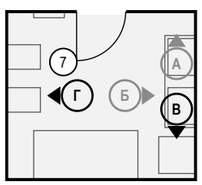


### Ведомость отделки (на листе)

| Марка | Поверхность | Материал, изделие | Цвет, код | Кол. |
|---|---|---|---|---|
| О10 | стены | облицовка плиткой, Atlas Concorde Marvel Travertine, 600×1200×9 мм, A8UZ, затирка CG2WA | Atlas Concorde A8UZ «Marvel Travertine» | 15 м² |
| О11 | потолок | окраска, Tikkurila Luja 7, матовая, подготовка Q3 | Tikkurila V503 «Winter» | 8,4 м² |

Визуализация этой стены — лист 20




### Примечания


1. Размеры — в мм от чистовых поверхностей стен; условные обозначения и общие указания — лист 27.
2. Стена Г показана двумя видами: здесь — архитектурная развёртка (мебель, отделка, проёмы, высоты), электроточки и выводы ВК с привязками и таблицей — на листе 103 («Привязки»).
3. Схема мебели, приборов и декора не является технической документацией для производства мебели; габариты — по паспортам изделий.
4. Облицовка — по сетке швов 2 мм, раскладка от оси стены (треугольник у пола), по высоте — от середины облицовки, подрезки у пола и у потолка поровну; подрезки — по листу раскладки плитки.
5. Гидроизоляция в 2 слоя, заход на стены 200 мм; над ванной — до 2000 и 300 мм за борт — до облицовки, с актом скрытых работ и тестом проливом (узел — на листе узлов).

| | | | | | | |
|---|---|---|---|---|---|---|
| | | | | | Проект: Квартира с кабинетом | М 1:20 |
| | Лист | № док. | Подпись | Дата | | |
| Дизайнер | Кырлан А.С. | | | 04.11.26 | Развёртки стен В, Г. Ванная (пом. 7) | Стадия: П; Лист: 102; Листов: 127 |

## Развёртка стены Б: электроточки и выводы

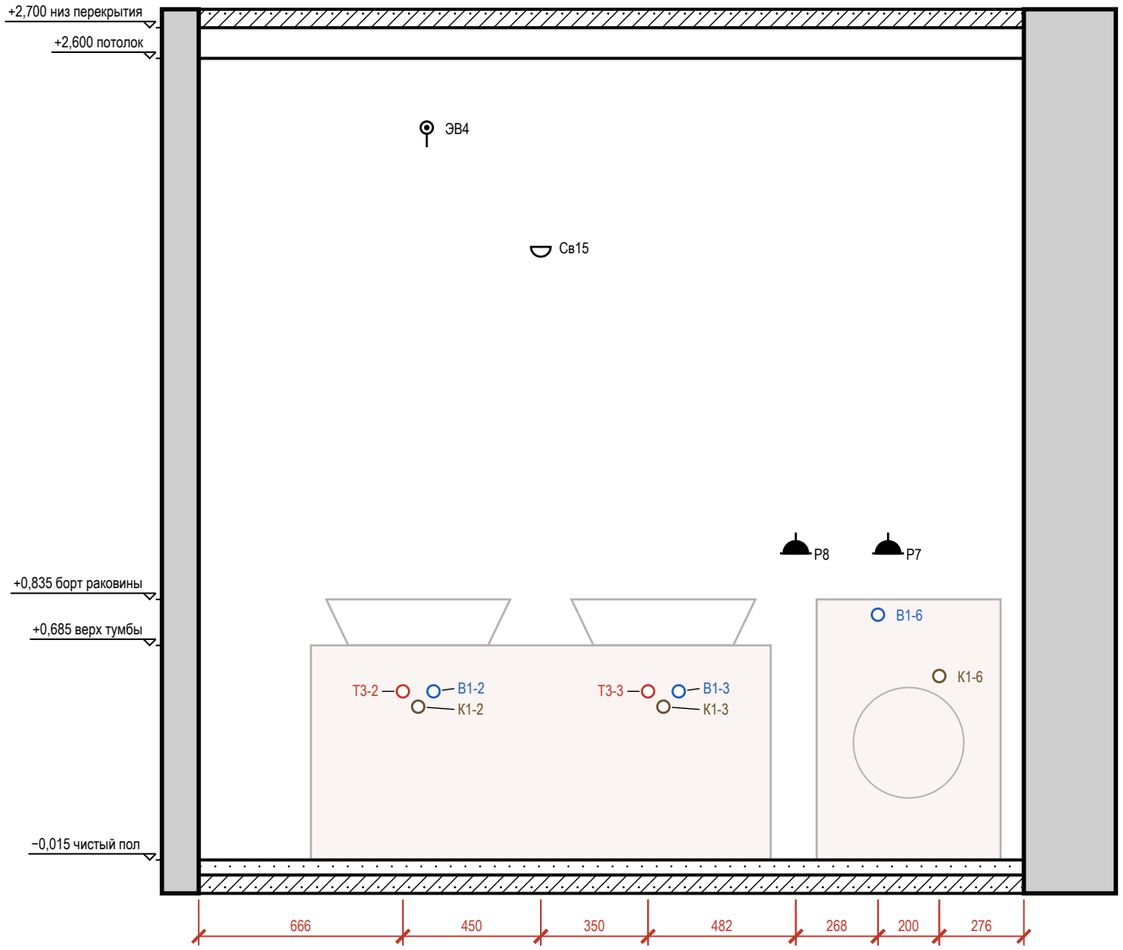


## Развёртка стены Г: электроточки и выводы

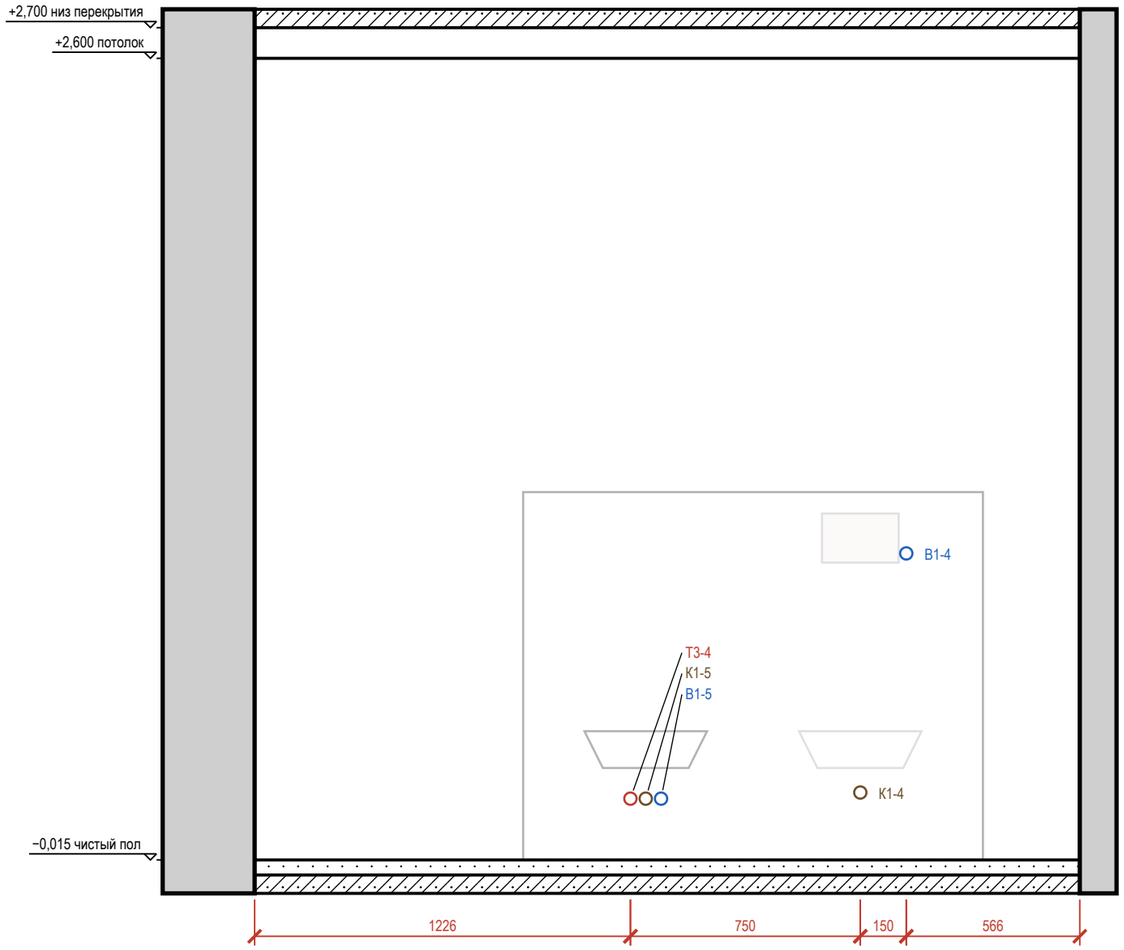


### Таблица привязок электроточек и выводов

| Стена | Марка | Назначение | От угла, мм | H от пола, мм | Примечание |
|---|---|---|---|---|---|
| Б | T3-2 | горячая вода — умывальник | 666 | 550 | межос. 100 |
| Б | K1-2 | канализация — умывальник | 716 | 500 | Ø50 |
| Б | ЭВ4 | вывод кабеля: вентилятор ВР1 (таймер выбега) | 744 | 2389 | гр. 3 |
| Б | B1-2 | холодная вода — умывальник | 766 | 550 | межос. 100 |
| Б | Св15 | светильник настенный | 1116 | 2000 | гр. 3 |
| Б | T3-3 | горячая вода — умывальник | 1466 | 550 | межос. 100 |
| Б | K1-3 | канализация — умывальник | 1516 | 500 | Ø50 |
| Б | B1-3 | холодная вода — умывальник | 1566 | 550 | межос. 100 |
| Б | P8 | розетка: фен у умывальника | 1948 | 1000 | гр. 13, IP44 |

| Стена | Марка | Назначение | От угла, мм | H от пола, мм | Примечание |
|---|---|---|---|---|---|
| Б | B1-6 | холодная вода — стиральная машина | 2216 | 800 | кран машины |
| Б | P7 | розетка: стиральная машина | 2249 | 1000 | гр. 12, IP44 |
| Б | K1-6 | канализация — стиральная машина | 2416 | 600 | Ø50 |
| Г | T3-4 | горячая вода — биде подвесное | 1226 | 200 | межос. 100, в раме |
| Г | K1-5 | канализация — биде подвесное | 1276 | 200 | Ø50 |
| Г | B1-5 | холодная вода — биде подвесное | 1326 | 200 | межос. 100, в раме |
| Г | K1-4 | канализация — унитаз подвесной | 1976 | 220 | Ø110 |
| Г | B1-4 | холодная вода — унитаз подвесной | 2126 | 1000 | в раме инсталляции |

### Условные обозначения

- розетка влагозащищённая IP44
- вывод кабеля для подключения прибора (без розетки), марка ЭВ
- светильник настенный (бра), H — высота оси
- вывод B1 (код — в ведомости привязок)
- вывод T3 (код — в ведомости привязок)
- вывод K1 (код — в ведомости привязок)
- привязки точек и выводов от угла и от пола, мм


### Примечания

1. Вид «Привязки» стен Б, Г — электроточки и выводы ВК; архитектурная развёртка (мебель, отделка, проёмы, высоты) — на листах 101, 102. Мебель и приборы подложкой для ориентира; их марки и обозначения мебели, проёмов и стен — там же.
2. Привязки — в мм: по горизонтали от левого чистового угла стены до оси изделия, H — от чистого пола до оси; все точки — в таблице привязок. Красная цепочка — привязки по осям; точки ближе 120 мм одна к другой в цепочку не дробятся — их привязки только в таблице.
3. У знака — марка электроточки (P — розетка, S — выключатель, Св — светильник, ЭВ — вывод кабеля); условные обозначения и общие указания — лист 27.
4. Коды выводов ВК: B1 — холодная вода, T3 — горячая вода, K1 — канализация; номер после дефиса — номер вывода на листе выводов сантехники.

| | | | | | |
|---|---|---|---|---|---|
| | | | | | Проект: Квартира с кабинетом — **М 1:20** |
| | Лист | № док. | Подпись | Дата | Привязки электроточек и выводов ВК, стены Б, Г. Ванная (пом. 7) |
| Дизайнер | Кырлан А.С. | | | 04.11.26 | Стадия: П; Лист: 103; Листов: 127 |


выпуск 04.11.2026 № 627e1ac6ce · стр. 103 из 127

## Развёртка стены Б

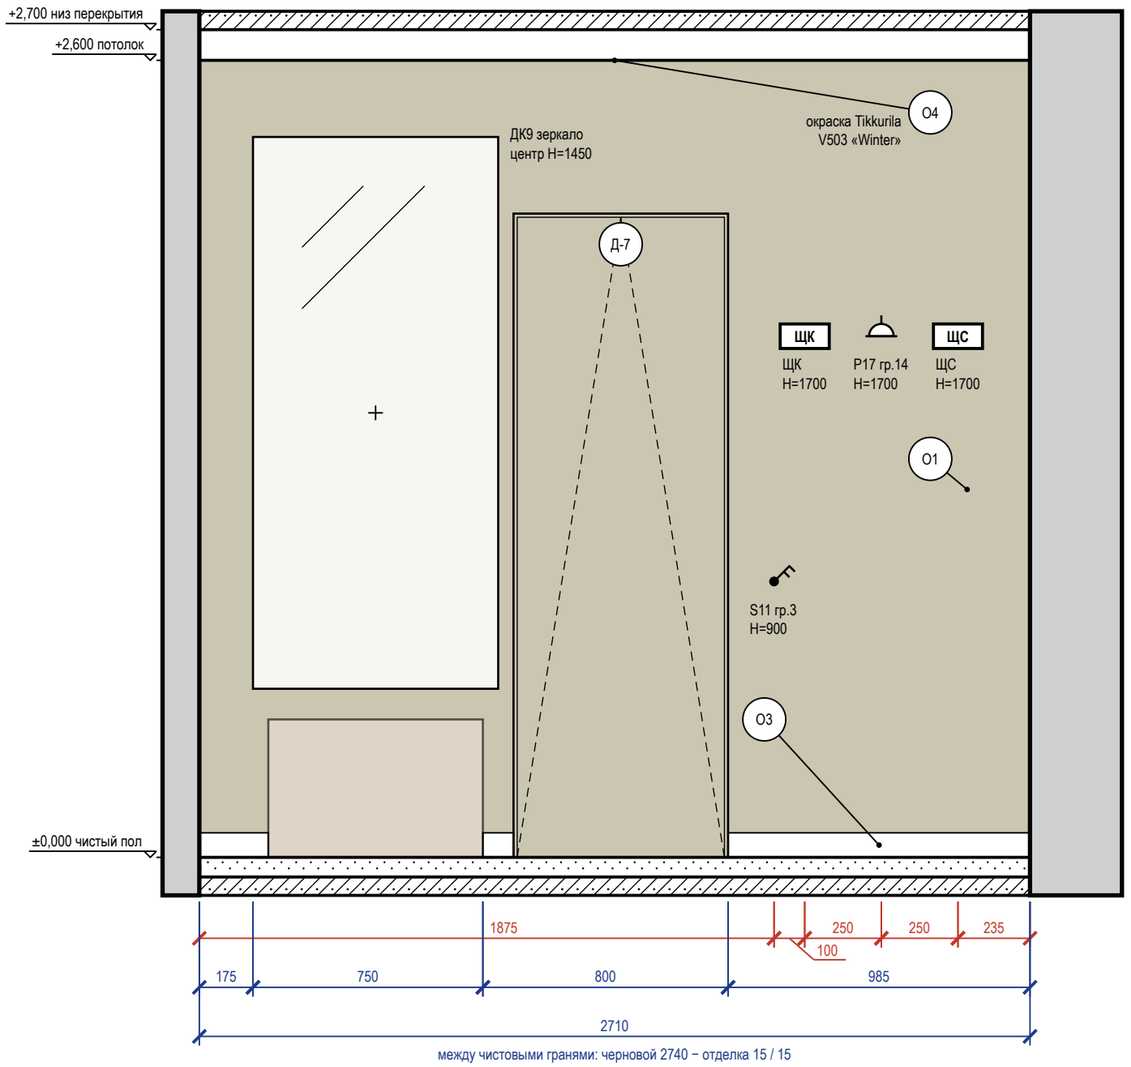



между чистовыми гранями: черновой 2740 − отделка 15 / 15

## Развёртка стены В

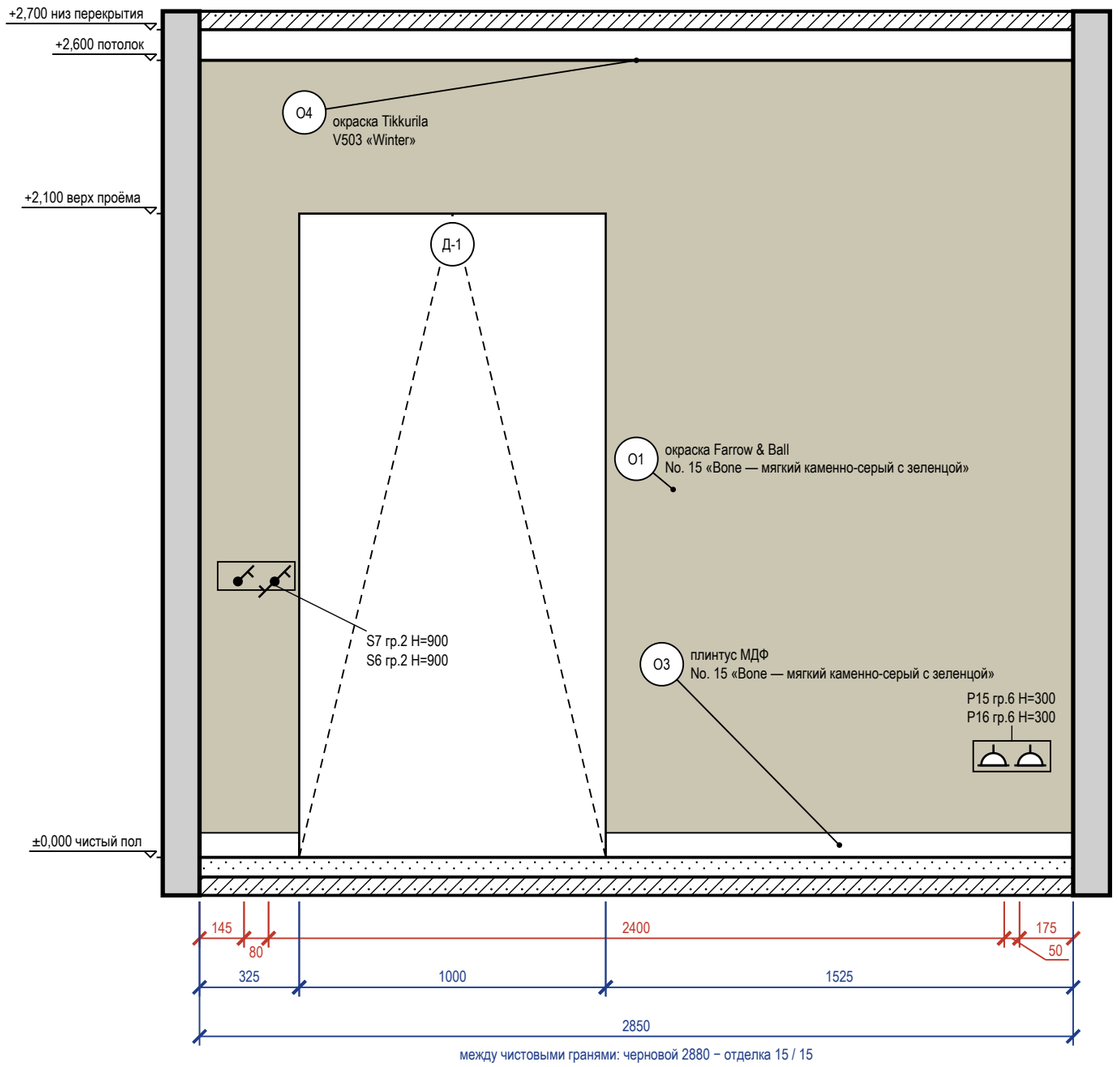


между чистовыми гранями: черновой 2880 − отделка 15 / 15


### Схема развёрток (М 1:100)

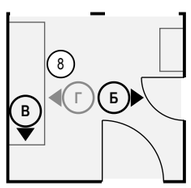


### Ведомость отделки (на листе)

| Марка | Поверхность | Материал, изделие | Цвет, код | Кол. |
|---|---|---|---|---|
| О1 | стены | окраска, Farrow & Ball Modern Emulsion, матовая, подготовка Q3 | Farrow & Ball No. 15 «Bone — мягкий каменно-серый с зеленцой» | 10,9 м² |
| О3 | плинтус | плинтус МДФ, h 80 мм, аналог: плинтус МДФ под покраску 80×16 | Farrow & Ball No. 15 «Bone — мягкий каменно-серый с зеленцой» | 3,2 м |
| О4 | потолок | окраска, Tikkurila Anti-Reflex 2, глубокоматовая, подготовка Q3 | Tikkurila V503 «Winter» | 7,9 м² |

Визуализация этой стены — лист 22

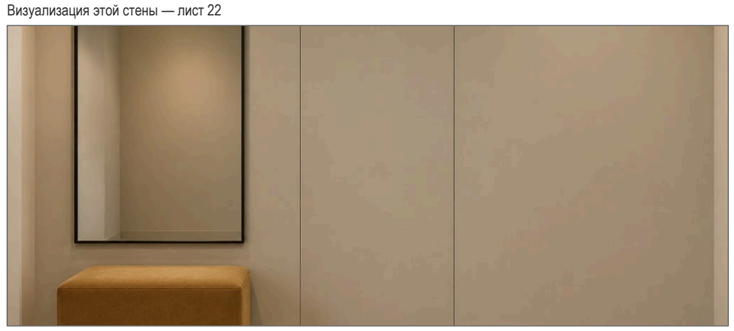


### Примечания

1. Размеры — в мм от чистовых поверхностей стен; условные обозначения и общие указания — лист 27.
2. Картины и зеркала крепить к основанию по паспорту изделия (закладные и анкеры — в перечне скрытых работ); крест — ось центра предмета.
3. Двери скрытого монтажа — полотно в плоскости стены, отделка стены по полотну, плинтус прерывается у короба (узел — на листе узлов).


| | | | | | | |
|---|---|---|---|---|---|---|
| | | | | | Проект: Квартира с кабинетом | М 1:20 |
| | Лист | № док. | Подпись | Дата | Развёртки стен Б, В. Прихожая (пом. 8) | Стадия / Лист / Листов |
| Дизайнер | Кырлан А.С. | | | 04.11.26 | | П / 104 / 127 |

выпуск 04.11.2026 № 627e1ac6ce · стр. 104 из 127

## Развёртка стены Г

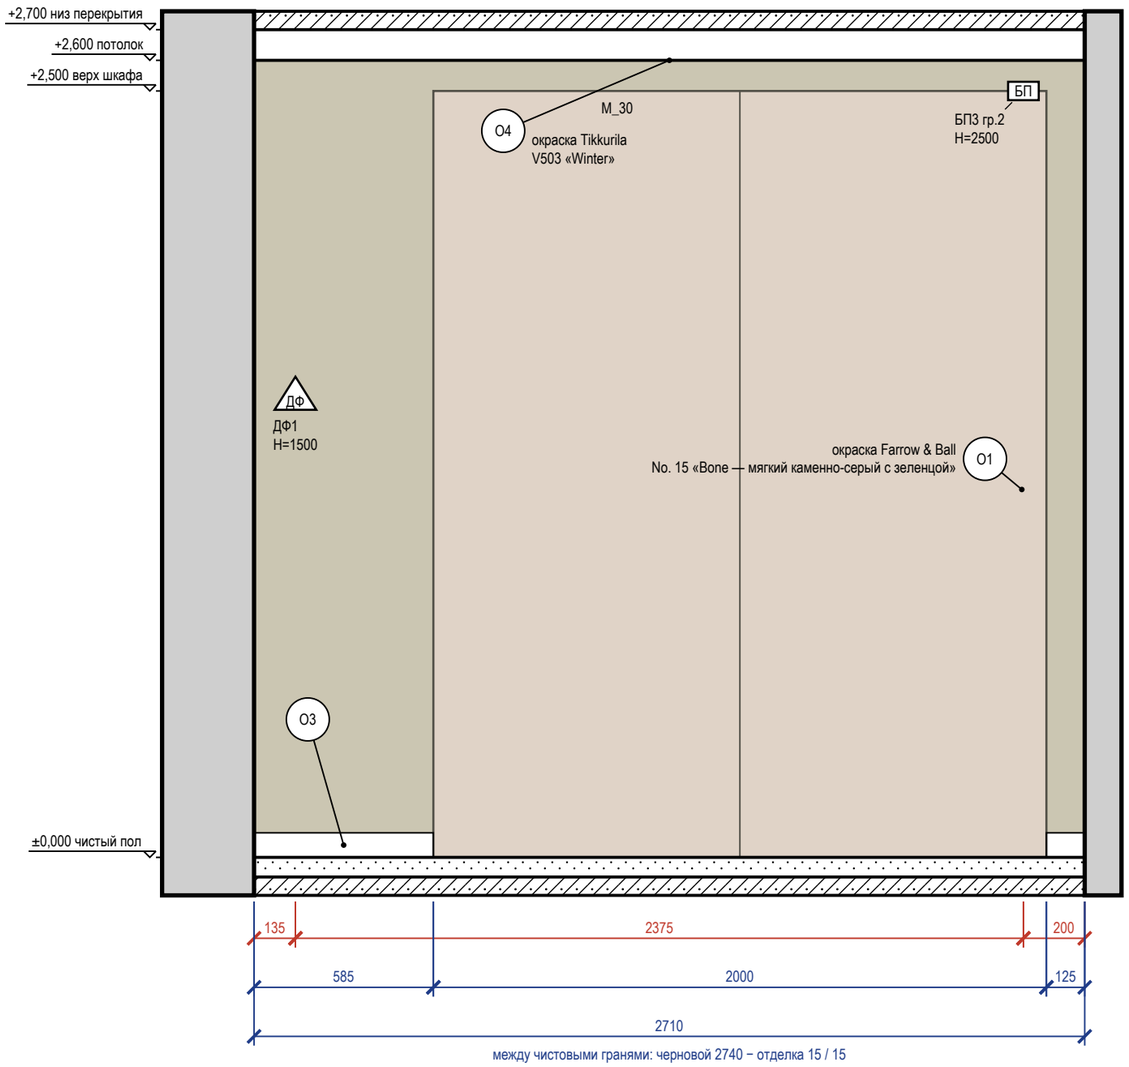


### Схема развёрток (М 1:100)

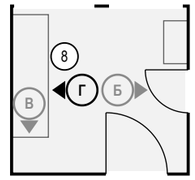


### Ведомость отделки (на листе)

| Марка | Поверхность | Материал, изделие | Цвет, код | Кол. |
|---|---|---|---|---|
| О1 | стены | окраска, Farrow & Ball Modern Emulsion, матовая, подготовка Q3 | Farrow & Ball No. 15 «Bone — мягкий каменно-серый с зеленцой» | 7 м² |
| О3 | плинтус | плинтус МДФ, h 80 мм, аналог: плинтус МДФ под покраску 80×16 | Farrow & Ball No. 15 «Bone — мягкий каменно-серый с зеленцой» | 0,7 м |
| О4 | потолок | окраска, Tikkurila Anti-Reflex 2, глубокоматовая, подготовка Q3 | Tikkurila V503 «Winter» | 7,9 м² |

Визуализация этой стены — лист 24




### Примечания

1. Размеры — в мм от чистовых поверхностей стен; условные обозначения и общие указания — лист 27.


| | | | | | |
|---|---|---|---|---|---|
| | Лист | № док. | Подпись | Дата | Проект: Квартира с кабинетом — М 1:20 |
| Дизайнер | Кырлан А.С. | | | 04.11.26 | Развёртка стены Г. Прихожая (пом. 8) |

| Стадия | Лист | Листов |
|---|---|---|
| П | 105 | 127 |


## Развёртка стены А

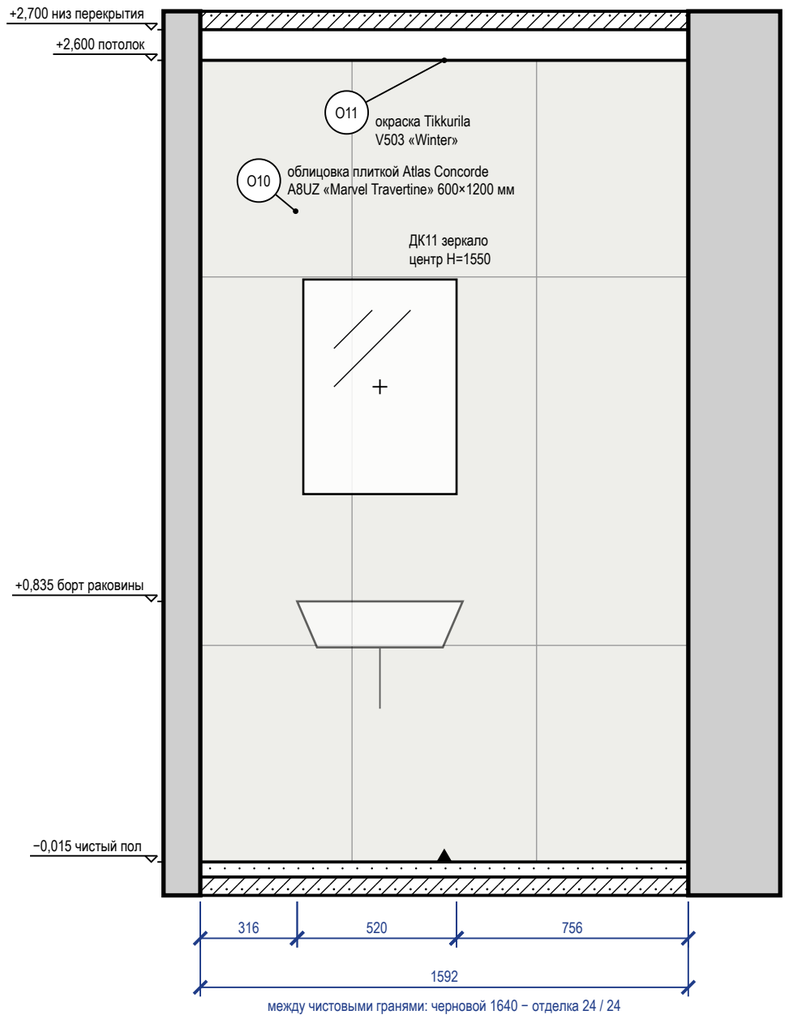


## Развёртка стены Б

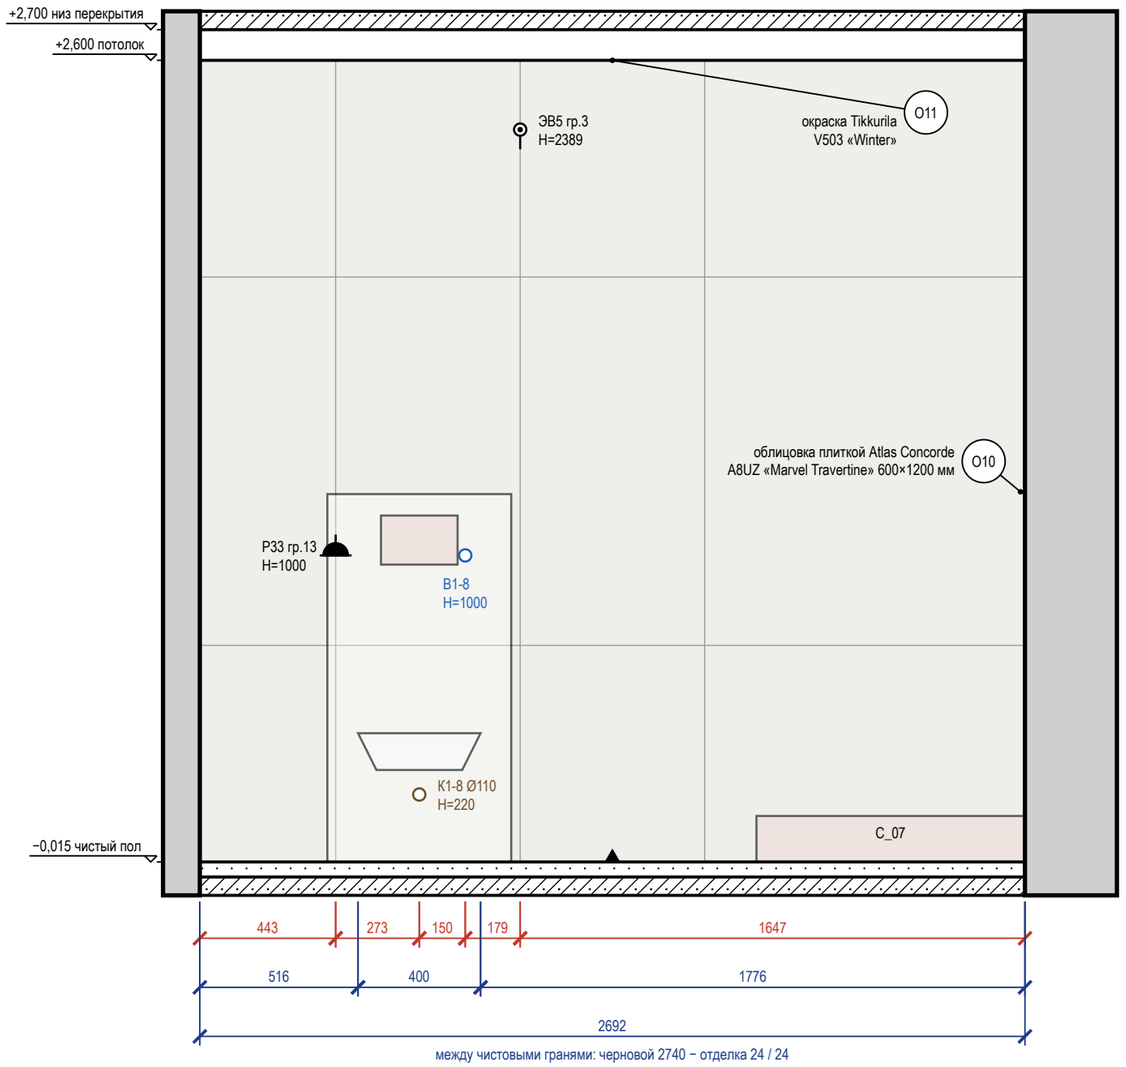


### Схема развёрток (М 1:100)

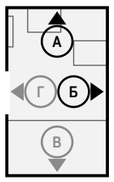


### Ведомость отделки (на листе)

| Марка | Поверхность | Материал, изделие | Цвет, код | Кол. |
|---|---|---|---|---|
| О10 | стены | облицовка плиткой, Atlas Concorde Marvel Travertine, 600×1200×9 мм, A8UZ, затирка CG2WA | Atlas Concorde A8UZ «Marvel Travertine» | 11,2 м² |
| О11 | потолок | окраска, Tikkurila Luja 7, матовая, подготовка Q3 | Tikkurila V503 «Winter» | 4,5 м² |

Визуализация этой стены — лист 26




### Примечания

1. Размеры — в мм от чистовых поверхностей стен; условные обозначения и общие указания — лист 27.
2. Стена А показана двумя видами: здесь — архитектурная развёртка (мебель, отделка, проёмы, высоты), электроточки и выводы ВК с привязками и таблицей — на листе 107 («Привязки»).
3. Схема мебели, приборов и декора не является технической документацией для производства мебели; габариты — по паспортам изделий.
4. Облицовка — по сетке швов 2 мм, раскладка от оси стены (треугольник у пола), по высоте — от середины облицовки, подрезки у пола и у потолка поровну; подрезки — по листу раскладки плитки.
5. Гидроизоляция в 2 слоя, заход на стены 200 мм; у душа — на всю высоту стен душевой зоны и 500 мм за край душевой зоны — до облицовки, с актом скрытых работ и тестом проливом (узел — на листе узлов).
6. Картины и зеркала крепить к основанию по паспорту изделия (закладные и анкеры — в перечне скрытых работ); крест — ось центра предмета.

| | | | | | |
|---|---|---|---|---|---|
| | | | | | Проект: Квартира с кабинетом — М 1:20 |
| | Лист | № док. | Подпись | Дата | |
| Дизайнер | Кырлан А.С. | | | 04.11.26 | Развёртки стен А, Б. Санузел гостевой (пом. 9) |

| Стадия | Лист | Листов |
|---|---|---|
| П | 106 | 127 |

## Развёртка стены А: электроточки и выводы

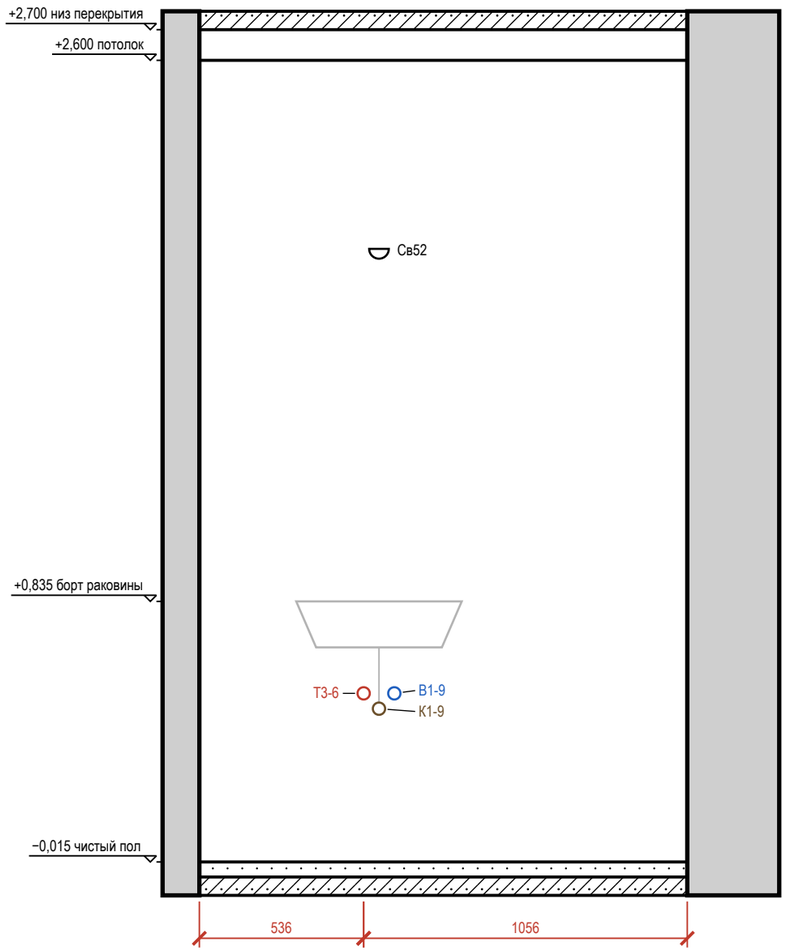



## Таблица привязок электроточек и выводов

| Марка | Назначение | От угла, мм | Н от пола, мм | Примечание |
|---|---|---|---|---|
| Т3-6 | горячая вода — умывальник | 536 | 550 | межос. 100 |
| К1-9 | канализация — умывальник | 586 | 500 | Ø50 |
| Св52 | светильник настенный | 586 | 2000 | гр. 3 |
| В1-9 | холодная вода — умывальник | 636 | 550 | межос. 100 |

## Условные обозначения

- светильник настенный (бра), Н — высота оси
- вывод В1 (код — в ведомости привязок)
- вывод Т3 (код — в ведомости привязок)
- вывод К1 (код — в ведомости привязок)
- привязки точек и выводов от угла и от пола, мм
- марка развёртки: буква стены, стрелка — взгляд

## Схема развёрток (М 1:50)

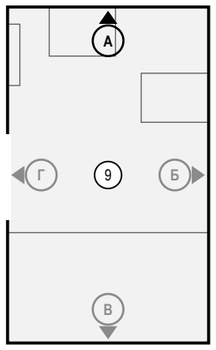



## Примечания

1. Вид «Привязки» стены А — электроточки и выводы ВК; архитектурная развёртка (мебель, отделка, проёмы, высоты) — на листе 106. Мебель и приборы — подложкой для ориентира; их марки и обозначения мебели, проёмов и стен — там же.
2. Привязки — в мм: по горизонтали от левого чистового угла стены до оси изделия, Н — от чистого пола до оси; все точки — в таблице привязок. Красная цепочка — привязки по осям; точки ближе 120 мм одна к другой в цепочку не дробятся — их привязки только в таблице.
3. У знака — марка электроточки (Р — розетка, S — выключатель, Св — светильник, ЭВ — вывод кабеля); условные обозначения и общие указания — лист 27.
4. Коды выводов ВК: В1 — холодная вода, Т3 — горячая вода, К1 — канализация; номер после дефиса — номер вывода на листе выводов сантехники.


| | | | | | | |
|---|---|---|---|---|---|---|
| | | | | | Проект: Квартира с кабинетом | М 1:20 |
| | Лист | № док. | Подпись | Дата | Привязки электроточек и выводов ВК, стена А. Санузел гостевой (пом. 9) | |
| Дизайнер | Кырлан А.С. | | | 04.11.26 | | |

| Стадия | Лист | Листов |
|---|---|---|
| П | 107 | 127 |


## Развёртка стены В

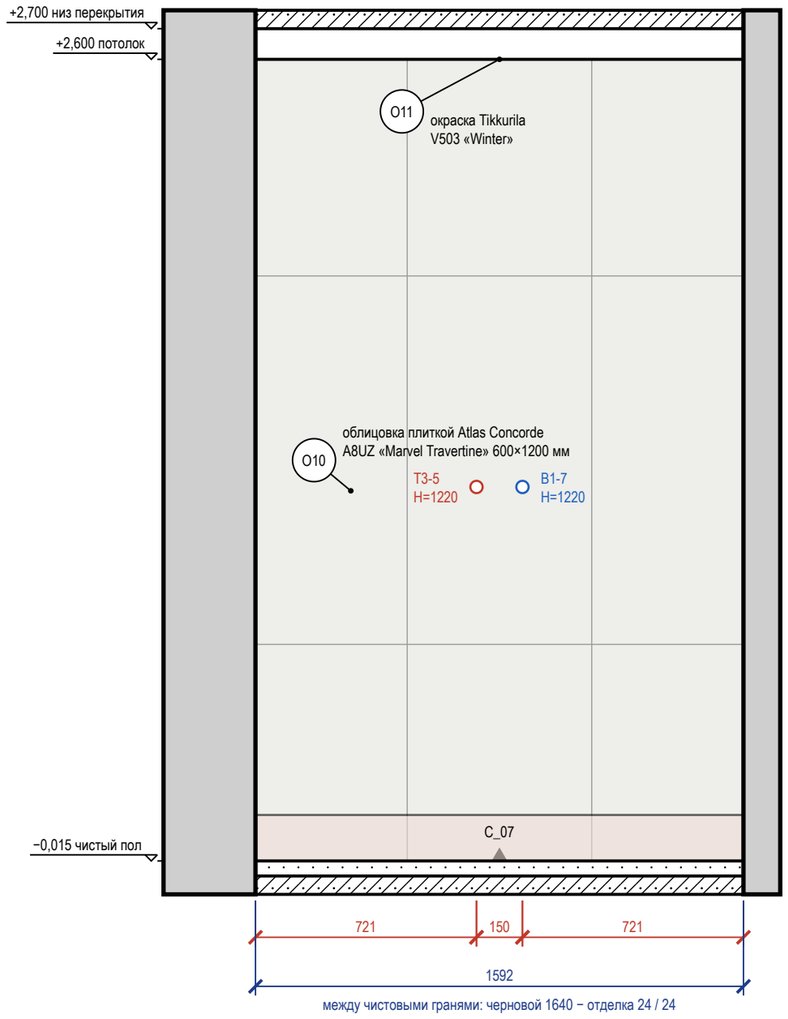


## Развёртка стены Г

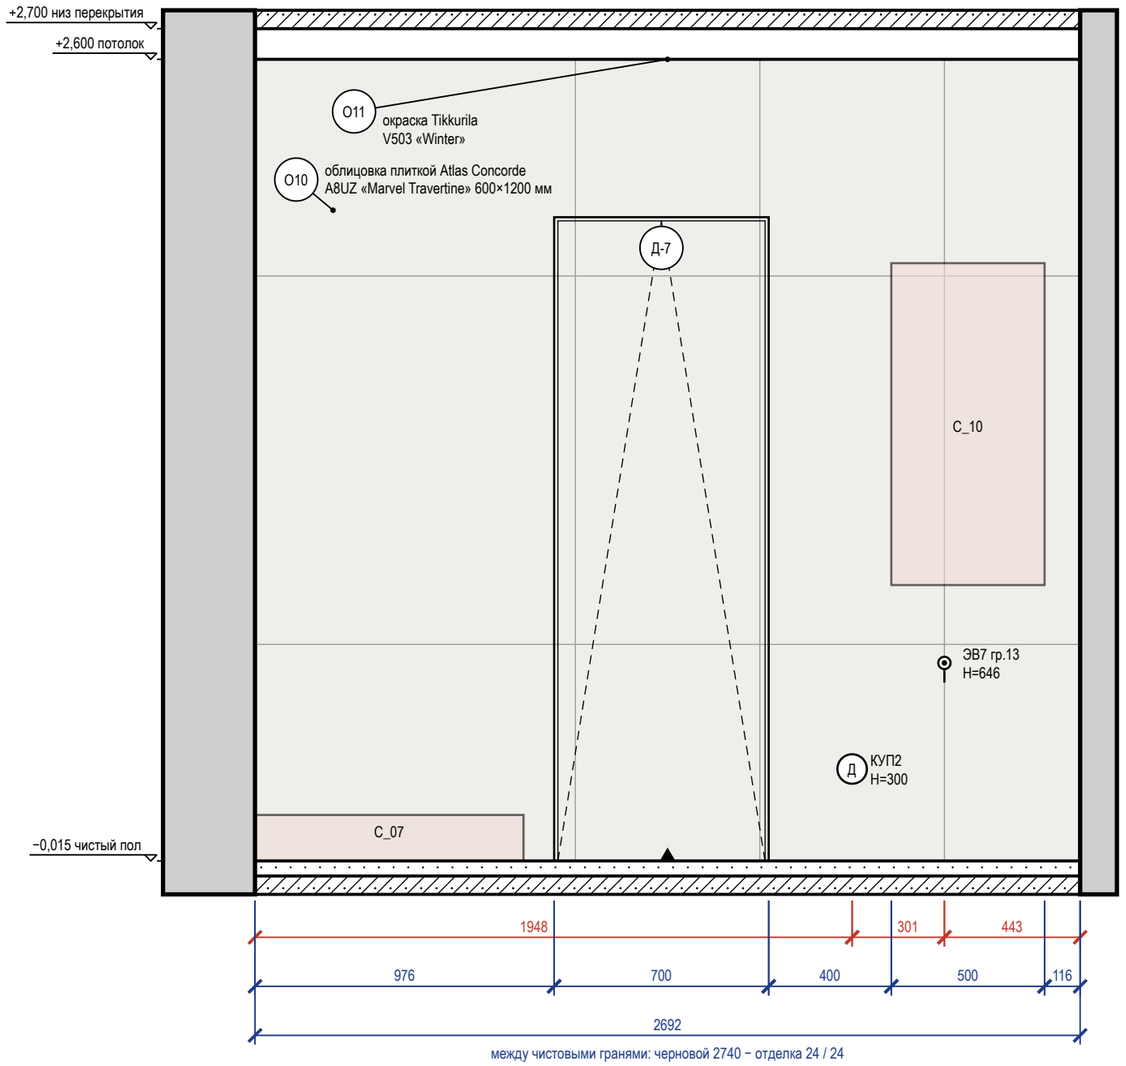


### Схема развёрток (М 1:100)

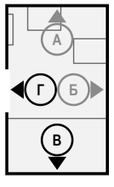


### Ведомость отделки (на листе)

| Марка | Поверхность | Материал, изделие | Цвет, код | Кол. |
|---|---|---|---|---|
| О10 | стены | облицовка плиткой, Atlas Concorde Marvel Travertine, 600×1200×9 мм, A8UZ, затирка CG2WA | Atlas Concorde A8UZ «Marvel Travertine» | 9,7 м² |
| О11 | потолок | окраска, Tikkurila Luja 7, матовая, подготовка Q3 | Tikkurila V503 «Winter» | 4,5 м² |

Визуализация этой стены — лист 25



### Примечания

1. Размеры — в мм от чистовых поверхностей стен; условные обозначения и общие указания — лист 27.
2. Схема мебели, приборов и декора не является технической документацией для производства мебели; габариты — по паспортам изделий.
3. Облицовка — по сетке швов 2 мм, раскладка от оси стены (треугольник у пола), по высоте — от середины облицовки, подрезки у пола и у потолка поровну; подрезки — по листу раскладки плитки.
4. Гидроизоляция в 2 слоя, заход на стены 200 мм; у душа — на всю высоту стен душевой зоны и 500 мм за край душевой зоны — до облицовки, с актом скрытых работ и тестом проливом (узел — на листе узлов).
5. Двери скрытого монтажа — полотно в плоскости стены, отделка стены по полотну, плинтус прерывается у короба (узел — на листе узлов).

| | | | | | |
|---|---|---|---|---|---|
| | | | | | Проект: Квартира с кабинетом — М 1:20 |
| | Лист | № док. | Подпись | Дата | Развёртки стен В, Г. Санузел гостевой (пом. 9) |
| Дизайнер | Кырлан А.С. | | | 04.11.26 | |

| Стадия | Лист | Листов |
|---|---|---|
| П | 108 | 127 |

выпуск 04.11.2026 № 627e1ac6ce · стр. 108 из 127

Комплект предварительный по пунктам этих таблиц. Пока по пункту нет ответа или решения, показанное на указанном листе — допущение проектировщика, а не утверждённое решение.
Сводка: открытых вопросов — 13 (из них ждут факта объекта — 4: контрольного обмера, обследования или документа); изменений в реестре — 9.

## Открытые вопросы и принятые допущения

| № | Формулировка | Вид | Кто решает | Если решения нет | Лист, где это проявляется |
|---|---|---|---|---|---|
| К-1 | Размеры квартиры сняты с растрового плана заказчика с частичными размерами (рисунок не в масштабе): помещения выровнены по подписанным размерам мебели и проходов. До заказа мебели, дверей и материалов нужен контрольный обмер всех помещений и проёмов. | Отсутствует<br>Ждёт: обмера | Архитектор-планировщик | размеры на листах — по плану заказчика, уточняются по месту; мебель на заказ и материалы по ним не заказывать | л. 30 — План планировки от заказчика<br>л. 37 — План размещения мебели и оборудования |
| К-2 | Высота потолка на плане заказчика не указана, принята 2700 мм. | Отсутствует | Архитектор-планировщик | высоты на развёртках и потолки — от 2700 мм, уточнить при обмере | л. 30 — План планировки от заказчика<br>л. 57 — План потолков |
| К-4 | Разрешённая мощность квартиры по ТУ неизвестна, принята 15 кВт. | Отсутствует | Инженер-электрик | щит и группы рассчитаны на 15 кВт; при меньших ТУ пересчёт | л. 63 — Однолинейная схема щита<br>л. 65 — План розеток и электровыводов |
| К-5 | Перепланировка (гардеробная-постирочная при спальне, Г-образный коридор, широкий проём прихожая — гостиная, гостевой санузел у прихожей) — предложение проектировщика: несущие стены дома неизвестны. Нужны поэтажный план БТИ / техзаключение и решение заказчика. | Отсутствует<br>Ждёт: документа | Архитектор-планировщик | перегородки и проёмы — предложение, к строительству не выдаются; мокрые зоны и кухня оставлены на местах плана заказчика | л. 30 — План планировки от заказчика |
| К-6 | Климатический подрайон (СП 131.13330) не задан: принят не северный — жилые комнаты и кухня под потолком от 2,5 м (СП 54, п. 5.12); в IA, IБ, IГ, IД, IVA — от 2,7 м. | Отсутствует<br>Ждёт: документа | Архитектор-планировщик | отметки потолков жилых — по 2,5 м; при северном подрайоне уровни ниже 2,7 м пересчитать до заказа каркаса | л. 57 — План потолков |
| К-7 | Проёмы скрытых дверей Д-2 … Д-7 по плану заказчика высотой 2100 мм, полотно расчётное 2000 мм (ряд UNION FILO-60 Piatto). По каталогам скрытых систем проём под полотно 2000 — 2050–2080 мм, под полотно 2100 — 2150–2180 мм: при проёме 2100 полотно 2000 оставляет над собой лишние 20–50 мм, полотно 2100 не входит. Решить по выбранной модели: проём по высоте 2050–2080 мм под полотно 2000 (как уменьшать — по узлу выбранной модели) или взять полотно 2100 с проёмом 2150–2180 мм (только в ненесущей стене, после контрольного обмера К-1). | Спорно<br>Ждёт: решения | Архитектор-планировщик | проёмы остаются 2100 мм, полотна «расч.» 2000 мм; двери до решения не заказывать | л. 55 — План размещения дверей<br>л. 30 — План планировки от заказчика |
| К-8 | Входная дверь Д-1 (проём 1000 × 2100 мм по плану заказчика): стальной дверной блок не выбран — размер блока и монтажный зазор (ГОСТ 31173-2016) из проёма не выводятся, на листах «блок — задать». Выбрать блок (изготовитель, модель, размер блока, открывание наружу, класс прочности и теплозащиты) и сверить проём по каталогу изготовителя при контрольном обмере (К-1). | Отсутствует<br>Ждёт: решения | Архитектор-планировщик | блок не заказывать, проём не изменять; на листах «блок задать» | л. 55 — План размещения дверей<br>полный альбом |
| К-10 | Душ С_07 с трапом (пом. 9, санузел гостевой, по плану заказчика — «душ с трапом и стеклянной перегородкой»): в стяжке 35 мм с облицовкой 14 мм трап не встаёт — монтажная высота трапа ≈ 90 мм от плиты до верха решётки (по паспорту модели) + уклон отвода Ø50 кратчайшим путём вдоль стен до стояка Ст К1-1 (3,11 м × 25 мм/м = 78 мм) = 168 мм при врезке на уровне плиты; врезка выше плиты поднимает подиум на столько же — отметку врезки замерить (К-1). Предложение проектировщика: душевая зона 900 × 1640 у стены В, подиум 120 мм у трапа (решётка +0,105), ступень по открытому краю 127 мм (уклон 15 мм/м к трапу); гидроизоляция по плите под подиумом и по подиуму, весь санузел; отвод от трапа в подиуме — к стене, за краем подиума — в коробе 160×110 вдоль стены до стояка (узел 1 на схеме разводки); смеситель — 1100 мм от пола душа. Расстановкой не решено: край подиума — в 100 мм от проёма Д-7; не помогает: та же зона глубиной 800 — край в 200 мм; зона 900 × 900 в углу В/Г — край в 100 мм. Решить: (а) зона 900 × 900 в углу В/Б — край в 747 мм от проёма, подиум 110 мм у трапа, ступень 117 мм, отвод 2,74 м; у проёма остаётся пол 740 × 900; кадры визуализации санузла перерисовать; (б) проём Д-7 сдвинуть от зоны (решение архитектора, обмер К-1); (в) оставить зону как есть: ступень у проёма осознанно, кромка ступени контрастная, подсветка у пола. Альтернативы по высоте: низкий поддон на ножках (сифон над полом), сверхплоский трап от 70 мм (подиум 100 мм) или подъём пола всего санузла с порогом. | Спорно<br>Ждёт: обмера, затем решения | Инженер ВК (вода, канализация) | трап и подиум не выполнять, пол санузла 9 до решения не стяжать; гидроизоляцию — по листу | л. 42 — План выводов сантехники<br>л. 43 — Схема разводки водопровода и канализации<br>л. 72 — План покрытий пола |
| К-11 | Ванна С_01 отдельностоящая со смесителем напольным (пом. 7, ванная, по заказчику): подвод ХВ и ГВ к стойке и выпуск Ø50 идут из пола, а стяжка ванной 35 мм их не укрывает — под водопровод Ø20 в полу нужно ≥ 65 мм (Ø + 45, СП 29.13330, п. 8.2), под выпуск Ø50 до стояка Ст К1-2 (3,6 м × 25 мм/м = 90 мм) — ≥ 185 мм. Решить: (а) подъём пола ванной до 185 мм (порог у двери, пересчёт высот выводов и развёрток), (б) смеситель настенный на стене В (выводы ХВ, ГВ на стене) и выпуск ванны к стене открытым сифоном, (в) смеситель на борт ванны. Место стойки на листах — предложение проектировщика. | Спорно<br>Ждёт: решения | Инженер ВК (вода, канализация) | выводы и выпуск ванны С_01 не выполнять, ванну и смеситель не заказывать; остальные выводы ванной — по листу | л. 42 — План выводов сантехники<br>л. 43 — Схема разводки водопровода и канализации<br>л. 52 — Спецификация сантехнического оборудования |
| К-12 | Проверяющий («Пров.») и нормоконтролёр («Н. контр.») комплекта не назначены: графы штампа пусты на всех листах, данные проекта и данные проекта не заданы. Их заполняет только человек, отличный от разработчика: разработчик подписи за них не ставит. Нужно решение автора — кто проверяет и кто ведёт нормоконтроль (фамилии, разные люди), и дата проверки. | Отсутствует<br>Ждёт: решения | Нормоконтролёр | графы «Пров.» и «Н. контр.» остаются пустыми; комплект предварительный, к производству работ не выдаётся | л. 27 — Список листов |
| К-17 | Циркуляция ГВС в данных не задана — циркуляционного трубопровода на схеме нет. Решить: нужна ли циркуляция | Отсутствует<br>Ждёт: решения | Инженер ВК (вода, канализация) | циркуляции на схеме нет | л. 47–50 — Развёртки мокрых зон: выводы ВК. Кухня-гостиная<br>л. 44 — Аксонометрическая схема В1 (холодное водоснабжение)<br>л. 43 — Схема разводки водопровода и канализации |

| | | | | | | |
|---|---|---|---|---|---|---|
| | | | | | Проект: Квартира с кабинетом | |
| | Лист | № док. | Подпись | Дата | Открытые вопросы, принятые допущения и конфликты. Лист 1 из 3 | Стадия / Лист / Листов |
| Дизайнер | Кырлан А.С. | | | 04.11.26 | | П / 109 / 127 |

## Открытые вопросы и принятые допущения (продолжение)

| № | Формулировка | Вид | Кто решает | Если решения нет | Лист, где это проявляется |
|---|---|---|---|---|---|
| К-19 | Кухня-гостиная (пом. 4, 45,5 м², два окна): мощность приборов не подтверждена расчётом — РО-5 500×600 (вынесен из модулей, ИЗ-6) и низкий РО-6 1400×200 под банкеткой-экраном (ИЗ-7, теплоотдача за экраном снижается). Нужен теплотехнический расчёт помещения (теплопотери через наружные стены и окна, параметры теплоносителя дома). При нехватке — вертикальный прибор на месте РО-5 или внутрипольный конвектор у окна 2 (решение ОВ). | Отсутствует | Инженер ОВ | РО-5 и РО-6 не заказывать до расчёта; места, подводки и экран — по листам | л. 71 — План отопления |
| К-20 | ТВ-стена М_24: низ ниши ТВ (+900) — в 150 мм над верхом ниши биокамина (+750). Телевизор и приставка на полке над топкой нагреваются; допустимое расстояние задают паспорта обеих моделей (биокамина — зона нагрева над топкой, телевизора температура эксплуатации). Варианты: (а) выбрать модели и подтвердить расстояние по паспортам; (б) поднять нишу ТВ (низ +1100 и выше — центр экрана выше уровня глаз сидящего); (в) развести ниши по ширине стены (камин сбоку от ТВ). Рекомендация исполнителя — (а), при нехватке расстояния — (б). | Спорно<br>Ждёт: решения | Мебельщик | нишу ТВ не изготавливать до выбора моделей; каркас и облицовку вне ниш — по листу | полный альбом<br>л. 92 — Развёртка стены В. Кухня-гостиная (пом. 4) |

## Изменения проекта после выпуска листов (реестр изменений)

| № | Дата | Лист | Было | Стало | Кто решил, подпись |
|---|---|---|---|---|---|
| ИЗ-1 | 26.10.2026 | л. 37 — План размещения мебели и оборудования<br>л. 38 — Спецификация мебели и оборудования<br>л. 41 — Ведомости изделий, техники и фурнитуры<br>полный альбом<br>л. 96 — Развёртка стены А. Детская (пом. 6)<br>л. 75 — Развёртка стены А. Спальня (пом. 1) | Шкаф-купе М_30 описан тремя разными изделиями (зеркальные арки / рифлёные панели / ЛДСП); М_08 «с арочными фасадами» без арки на чертеже; кровать детской М_27 на радиаторе РО-9 под окном, ковёр Т22 2500 × 1800 под ней; диван М_22 «угловой» нарисован прямым; у стола М_21 6 стульев, три из них — в банкетке М_20 (за стулом 150 мм). Спальня: шина штор Т1/Т2 одна, 300…2800 по стене А, на окно 1 — пакет штор заходил на окно 2, у окна 2 штор нет. | Предложения проектировщика, заказчиком не утверждены: М_30 — фасад МДФ 10 мм, эмаль матовая, профиль латунь матовая, зеркальные арочные вставки (поле 100 мм), как на кадре; М_08 — арочная фрезеровка филёнок (поле 100 мм); М_27 — кровать 800 × 2000 (было 900 × 2000) у стены Б, 1480 мм от угла с дверью: вне радиатора РО-9, от открытого полотна Д-5 620 мм прохода, вдоль кровати к окну 520 мм (кровать 900 между полотном и стеной В не встаёт: 600 + 900 + 500 > 1940 мм); М_22 — диван угловой Г 2700 × 1600; М_21 — банкетка М_20 на 3 места и 3 стула (2 со свободной стороны, 1 у торца). Т22 — ковёр 1200 × 1700 у кресла-кокона М_28 вместо ковра 2500 × 1800 под кроватью (кровать в 520 мм от стены В: ковёр под ней не выходит за кровать на 450 мм и не оставляет 200 мм пола у стены). До подписи — не заказывать. Знак «**» у М_08 не ставится: марка М_08 совпадает с кодом канализации М_08, и ядро поставило бы знак у каждого «М_08» на листах ВК; предложение по М_08 — только в этой записи. М_27 — изголовье 1000 мм от пола (до выбора модели); ДК2 — низ 1200 мм, на 200 над изголовьем (было 700 от матраса — картина за изголовьем). Спальня: в нише штор по стене А две шины по 2300 мм — Т1/Т2 на окно 1 (0…2300) и Т27/Т28 на окно 2 (2300…4600), верх +2,600 (верх ниши), длину — по обмеру ниши (К-1). Т1, Т2, Т27, Т28 — предложение: на листах со знаком «**», до подписи шины не заказывать. | Утверждено: Кырлан А.С., 01.11.2026.<br>Предложил: исполнитель. |
| ИЗ-2 | 30.10.2026 | л. 55 — План размещения дверей<br>л. 37 — План размещения мебели и оборудования<br>л. 42 — План выводов сантехники<br>л. 69 — Управление светильниками<br>л. 53 — Раскладка плитки. Ванная. Развёртки стен | Ванная (пом. 7): дверь Д-6 (800 мм, стена А, привязка 2300) открывалась внутрь — полотно на 90° задевало тумбу М_29 (привязка 450) и раковину С_02 (привязка 500): дверь не открыть, в выпуске для заказчика — ошибка; С_02 стояла в полосе 600 мм перед проёмом. Конфликт Кф-3 открыт. | Проём Д-6 сдвинут вдоль стены А от угла Б: привязка 2300 → 1200 (х 4900…5700), петли у х 4900, открывание внутрь, в сторону стены Г (там полотенцесушитель С_06 на стене А 500…1000 — не в секторе). Тумба М_29, раковины С_02, С_03, стиральная машина ОБ_03 остаются на местах; С_02 (500…1100) вне полосы 600 мм перед проёмом. Выключатель S13 в коридоре — к проёму (привязка 3550, со стороны ручки), коробка КУП1 на стене А — привязка 2300. Раскладка плитки стены А пересчитана движком. Знак «**» у Д-6 остаётся до подписи автора; Кф-3 — у владельца до подписи этой записи. | Утверждено: Кырлан А.С., 01.11.2026.<br>Предложил: исполнитель. |
| ИЗ-3 | 30.10.2026 | л. 37 — План размещения мебели и оборудования<br>полный альбом<br>л. 77 — Привязки электроточек, стена Б. Спальня (пом. 1) | Спальня (пом. 1): кресло-ракушка М_05 (х 600, у 3000, 750×750) перекрывало туалетный столик М_04 (стена В, 500…1700, глубина 450) на 200 мм — на плане кресло поверх столика, на визуализации — рядом; ни одно правило пересечения мебели это не ловило. | М_05 переставлено в угол у окна 1 (х 600…1350, у 600…1350), столик М_04 свободен; кадры спальни сверить с планом заново (views-check). Знак «**» у М_05 до подписи автора. | Утверждено: Кырлан А.С., 01.11.2026.<br>Предложил: исполнитель. |
| ИЗ-4 | 30.10.2026 | л. 37 — План размещения мебели и оборудования<br>л. 38 — Спецификация мебели и оборудования<br>л. 41 — Ведомости изделий, техники и фурнитуры<br>полный альбом | Марки мебели кабинета К1–К7 совпадали с позициями колерной карты К1–К8, марки прихожей П8, П9 — с сантехприборами П1–П13: марка неоднозначна в пределах комплекта. | Мебель кабинета — М_08, М_09, М_10, М_11, М_12, М_13, ОБ_02, мебель прихожей — М_30 (шкаф-купе), М_31 (банкетка); ссылки точек электрики, текстиля и декора переписаны вместе с марками. Колорист и ВК не тронуты. | Утверждено: Кырлан А.С., 02.11.2026.<br>Предложил: исполнитель. |



| | | | | | |
|---|---|---|---|---|---|
| | | | | | Проект: Квартира с кабинетом |
| | | | | | |
| | Лист | № док. | Подпись | Дата | Открытые вопросы, принятые допущения и конфликты. Лист 2 из 3 |
| Дизайнер | Кырлан А.С. | | | 04.11.26 | |

| Стадия | Лист | Листов |
|---|---|---|
| П | 110 | 127 |

## Изменения проекта после выпуска листов (реестр изменений) (продолжение)

| № | Дата | Лист | Было | Стало | Кто решил, подпись |
|---|---|---|---|---|---|
| ИЗ-5 | 01.11.2026 | л. 37 — План размещения мебели и оборудования<br>л. 41 — Ведомости изделий, техники и фурнитуры<br>полный альбом<br>л. 92 — Развёртка стены В. Кухня-гостиная (пом. 4) | ТВ-стена М_24 записана 30.10.2026 «автор: Кырлан А.С.» с нишами ТВ 1500×900 (низ +900) и биокамина 900×400 (низ +350) — размеры задал исполнитель, записи об изменении не было, на листе изделия Д_4 стена рисовалась шкафом с антресолями и штангой. | Предложение исполнителя, заказчиком не утверждено: М_24 — каркас из оцинкованного профиля на стене Б с облицовкой панелями МДФ 19 мм, эмаль; ниша ТВ 1500×900, низ +900, глубина 400, низ ниши — полка под приставку; ниша биокамина 900×400, низ +350 — облицовка негорючая (сталь 2 мм / камень), зазоры 50 мм до панелей — до паспорта модели (К-13). До подписи — не изготавливать. | Утверждено: Кырлан А.С., 01.11.2026.<br>Предложил: предложение исполнителя по наименованию. |
| ИЗ-6 | 01.11.2026 | л. 71 — План отопления<br>л. Д_9 — Кухня (пом. 4). Развёртка гарнитура<br>л. 89 — Привязки электроточек и выводов ВК, стена А. Кухня-гостиная (пом. 4) | Радиатор РО-5 выводился листом ОВ под окном 1 кухни (стена А, привязка 1050, 700×600) — внутри модулей М_16 (посудомоечная машина) и М_17 (ящики): экран невозможен. | РО-5 — на свободном участке наружной стены А между колонной М_14 и банкеткой М_20: привязка 3350, 500×600, низ +120 (х 11750…12250); гарнитур под окном 1 без прибора. Мощность 500-го прибора сверить теплотехническим расчётом ОВ (при нехватке — вертикальный прибор на том же месте); стояки и подводки отопления не замерены (К-1). Все радиаторы квартиры теперь в данных — одни и те же на листе ОВ, в мебели, DXF и IFC. | Утверждено: Кырлан А.С., 01.11.2026.<br>Предложил: исполнитель (ОВ). |
| ИЗ-7 | 01.11.2026 | л. 71 — План отопления<br>л. 41 — Ведомости изделий, техники и фурнитуры<br>л. 89 — Привязки электроточек и выводов ВК, стена А. Кухня-гостиная (пом. 4) | Банкетка М_20 у окна 2 — экран радиатора РО-6, выведенного листом ОВ 900×600 (низ +120, верх +720): прибор под сиденье банкетки не вставал, низ щита сиденья не задан. | РО-6 — низкий панельный прибор 1400×200 по ширине окна 2 (привязка 4400, низ +120, верх +320); банкетка М_20: сиденье +450, низ щита сиденья +400 (верх прибора + 80 мм), решётка в лицевой панели, щель 60 мм у стены. Мощность низкого прибора сверить теплотехническим расчётом ОВ (при нехватке — внутрипольный конвектор у окна). | Утверждено: Кырлан А.С., 01.11.2026.<br>Предложил: исполнитель (ОВ, мебель). |
| ИЗ-8 | 01.11.2026 | полный альбом<br>л. 70 — План вентиляции | Вытяжка над варочной панелью острова М_19 не была задана (К-9); предложение исполнителя — островная потолочная вытяжка в режиме рециркуляции — ждало решения. | Принято автором (ответ передан координатором): островная потолочная вытяжка 900 мм над М_19 в режиме рециркуляции (угольный фильтр), низ +1550. Вариант с отводом в вентканал ВК-3 не выбран: короба в потолке нет. После подписи автора вопрос К-9 закрывается, знак предложения снимается. Модель вытяжки не выбрана: крепление к перекрытию и вывод питания на потолке по паспорту модели. | Утверждено: Кырлан А.С., 01.11.2026.<br>Предложил: Александр Кырлан, решение автора. |
| ИЗ-9 | 01.11.2026 | л. 37 — План размещения мебели и оборудования<br>л. 41 — Ведомости изделий, техники и фурнитуры<br>полный альбом<br>л. 92 — Развёртка стены В. Кухня-гостиная (пом. 4) | Биокамин в ТВ-стене М_24: модель, мощность, зазоры и приток не заданы (К-13); до ответа нишу камина изготавливать было нельзя. | Принято автором (ответ передан координатором): биокамин в ТВ-стене М_24 остаётся, ниша 900×400, низ +350, облицовка негорючая (сталь 2 мм / камень), зазоры 50 мм до панелей. После подписи автора вопрос К-13 «оставлять ли биокамин» закрывается. Модель биокамина не выбрана: зазоры, тепловая мощность и приток воздуха (при мощности > 2 кВт — решение ОВ) уточняются по паспорту модели — пометка на листе остаётся. | Утверждено: Кырлан А.С., 01.11.2026.<br>Предложил: Александр Кырлан, решение автора. |


### Примечания

1. Номера листов — по ведомости рабочих чертежей комплекта (лист «Общие данные»).
2. Графа «Если решения нет» показывает состояние решения на листах; влияние на сроки и стоимость по пунктам не оценивалось.
3. Пункт, по которому принято решение, при следующем выпуске комплекта из таблиц исключается.




| | | | | | | | | |
|---|---|---|---|---|---|---|---|---|
| | | | | | Проект: Квартира с кабинетом | | | |
| | Лист | № док. | Подпись | Дата | Открытые вопросы, принятые допущения и конфликты. Лист 3 из 3 | Стадия | Лист | Листов |
| Дизайнер | Кырлан А.С. | | | 04.11.26 | | П | 111 | 127 |


## Общий вид

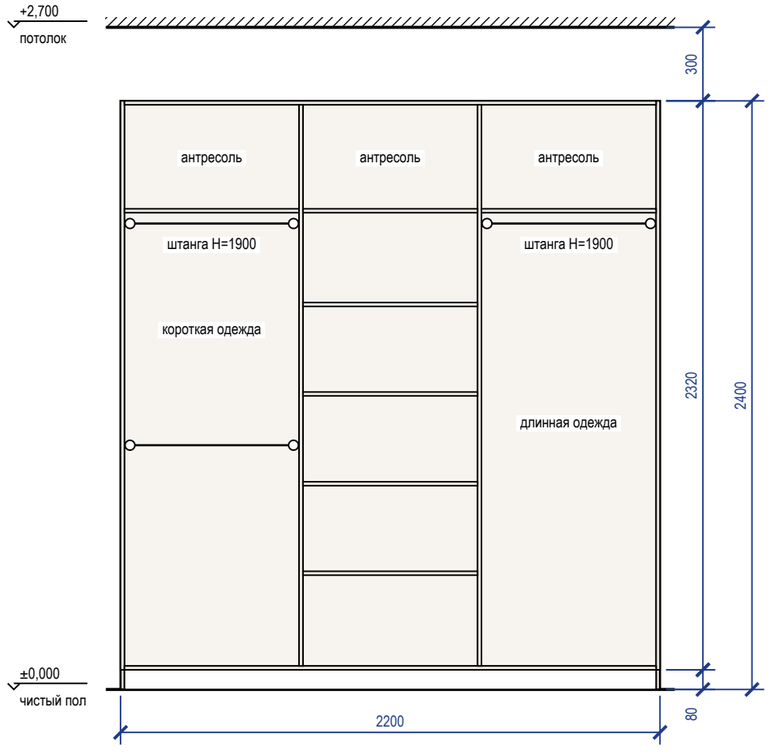



## Наполнение, размеры в свету

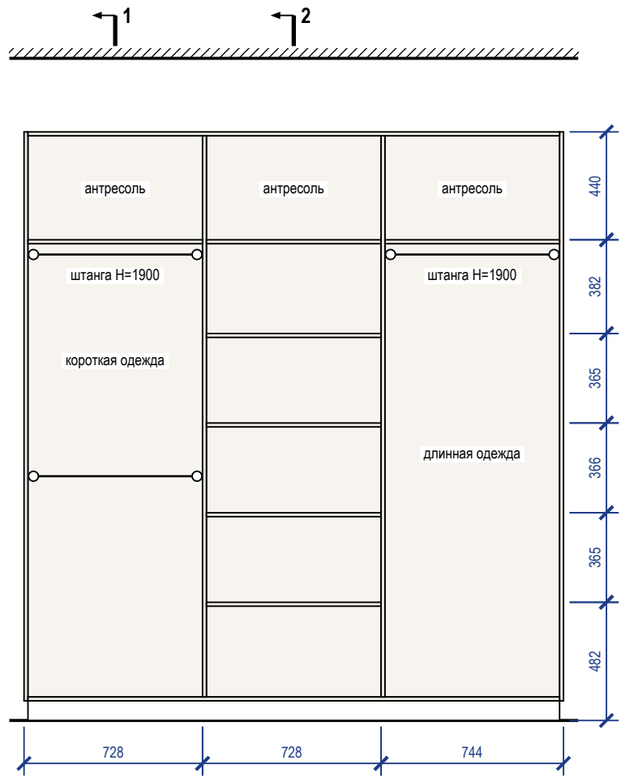


## Разрез 1-1

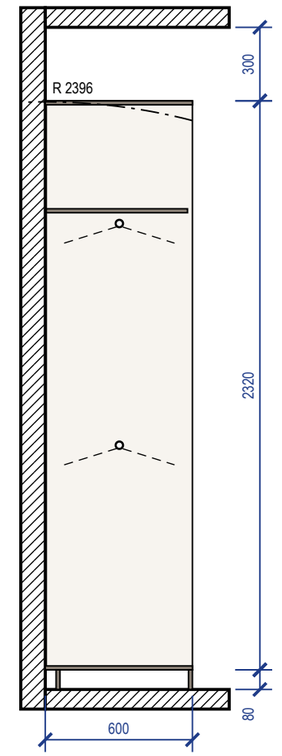



## Разрез 2-2

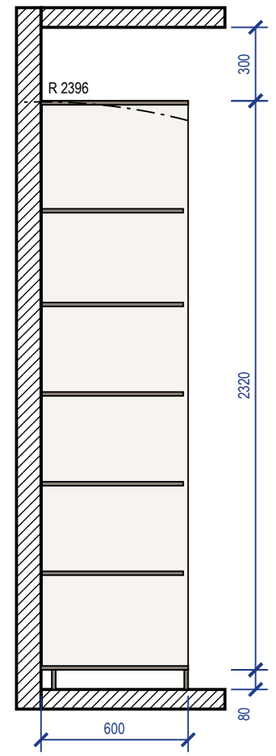


### Примечания


1. Размеры — в мм по чистовой отделке; изделие 2200×600×2400 (Ш×Г×В). Перед раскроем — контрольный замер цеха после чистовой отделки стен, пола и потолка.
2. Корпус — ЛДСП 16 мм, задняя стенка ХДФ 4 мм в паз, цоколь 80 мм на регулируемых опорах; открытая система: без фасадов.
3. Кромка: скрытые торцы 0,4 мм, видимые 2 мм (ПВХ/АБС).
4. Присадка по 32-й системе — выполняет цех.
5. Зазор до потолка 300 мм.
6. Подъём корпуса: диагональ боковины без цоколя √(2320² + 600²) = 2396 мм < 2700 мм до потолка — корпус собирается лёжа, поднимается поворотом и ставится на цоколь.
7. Крепление к стене от опрокидывания: крепление к стене, 3 точки; основание стены и шаг анкеров — монтажная схема шкафов.

## 3D орто

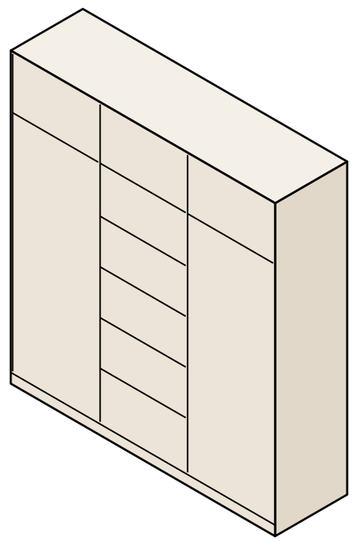


| | | | | | | |
|---|---|---|---|---|---|---|
| | | | | | Проект: Квартира с кабинетом | **М 1:25** |
| | Лист | № док. | Подпись | Дата | | |
| Дизайнер | Кырлан А.С. | | | 04.11.26 | Система хранения М_06 | Стадия: П; Лист: Д_1; Листов: 127 |


## Общий вид

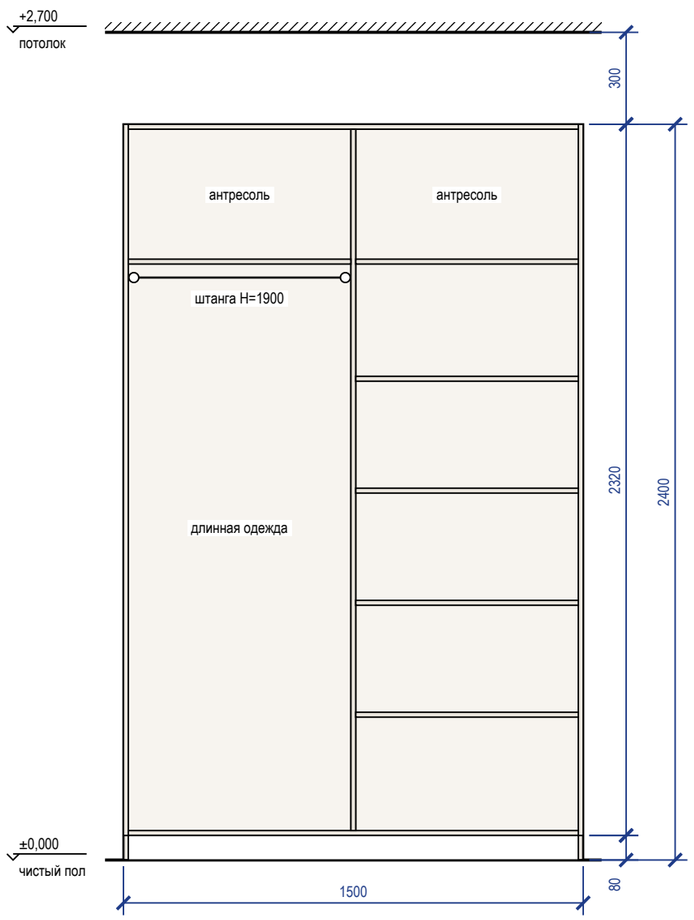



## Наполнение, размеры в свету

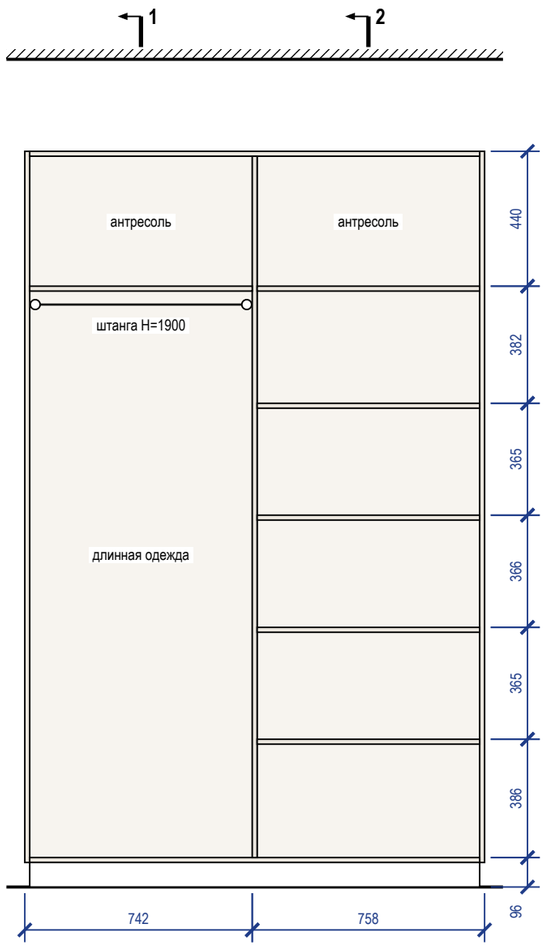


## Разрез 1-1

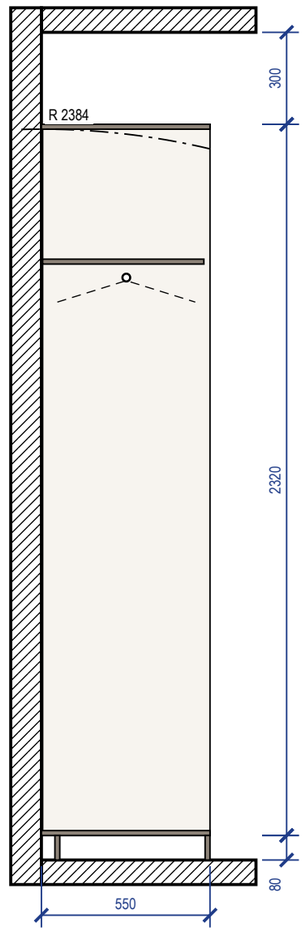



## Разрез 2-2

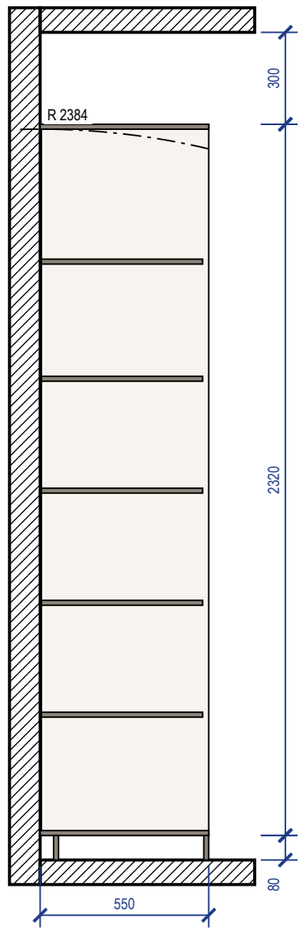


### Примечания

1. Размеры — в мм по чистовой отделке; изделие 1500×550×2400 (Ш×Г×В). Перед раскроем — контрольный замер цеха после чистовой отделки стен, пола и потолка.
2. Корпус — ЛДСП 16 мм, задняя стенка ХДФ 4 мм в паз, цоколь 80 мм на регулируемых опорах; открытая система: без фасадов.
3. Кромка: скрытые торцы 0,4 мм, видимые 2 мм (ПВХ/АБС).
4. Присадка по 32-й системе — выполняет цех.
5. Зазор до потолка 300 мм.
6. Подъём корпуса: диагональ боковины без цоколя $\sqrt{(2320^2 + 550^2)} = 2384$ мм < 2700 мм до потолка — корпус собирается лёжа, поднимается поворотом и ставится на цоколь.
7. Крепление к стене от опрокидывания: крепление к стене, 3 точки; основание стены и шаг анкеров — монтажная схема шкафов.


## 3D орто

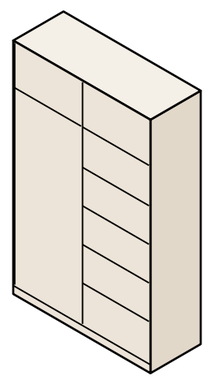


| | | | | | | |
|---|---|---|---|---|---|---|
| | | | | | Проект: Квартира с кабинетом | **М 1:20** |
| | Лист | № док. | Подпись | Дата | Система хранения М_07 | Стадия / Лист / Листов |
| Дизайнер | Кырлан А.С. | | | 04.11.26 | | П / Д_2 / 127 |

выпуск 04.11.2026 № 627e1ac6ce · стр. 113 из 127


## Вид с фасадами

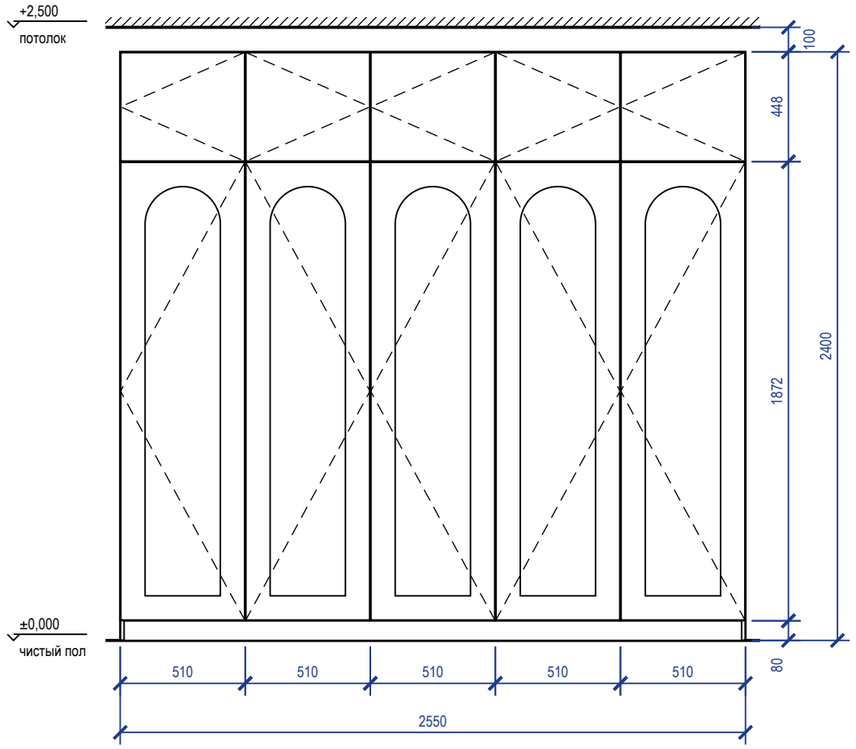



## Вид без фасадов

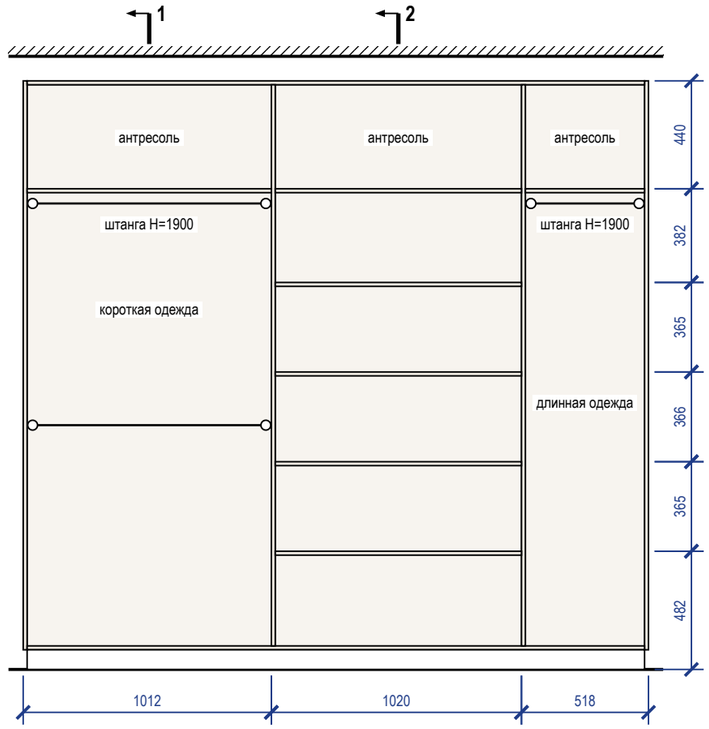


## Разрез 1-1

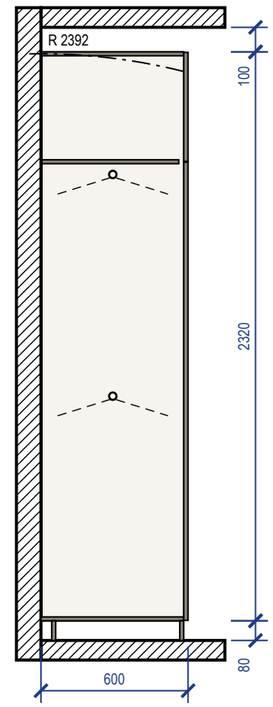



## Разрез 2-2

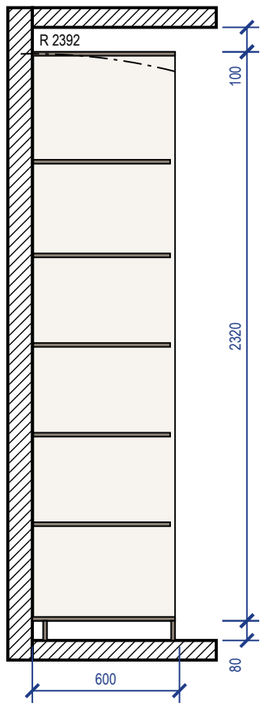


### Примечания

1. Размеры — в мм по чистовой отделке; изделие 2550×600×2400 (Ш×Г×В). Перед раскроем — контрольный замер цеха после чистовой отделки стен, пола и потолка.
2. Корпус — ЛДСП 16 мм, задняя стенка ХДФ 4 мм в паз, цоколь 80 мм на регулируемых опорах; фасады накладные — МДФ 18 мм, эмаль матовая; арочная фрезеровка филёнки (полукруглый верх, поле 100 мм); цвет — по колерной карте; петли с доводчиком: фасад 1869 мм — 4 петли, фасад 445 мм — 2 петли.
3. Кромка: скрытые торцы 0,4 мм, видимые 2 мм (ПВХ/АБС).
4. Номинальные зазоры: между фасадами 3 мм, фасад — стена и фасад — потолок не менее 3 мм, фасад ящика — стойка 2 мм.
5. Присадка по 32-й системе — выполняет цех.
6. Зазор до потолка 100 мм — закрыть планкой в цвет корпуса при монтаже.
7. Подъём корпуса: диагональ боковины без цоколя √(2320² + 582²) = 2392 мм < 2500 мм до потолка — корпус собирается лёжа, поднимается поворотом и ставится на цоколь.
8. Крепление к стене от опрокидывания — уголки 2 шт. к несущему основанию (монтажная схема шкафов).


## 3D орто

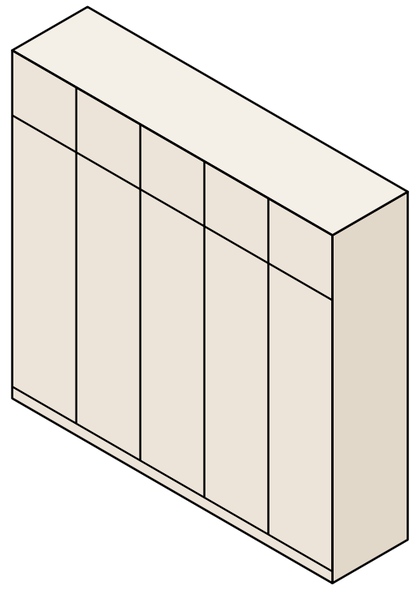


| | | | | | | |
|---|---|---|---|---|---|---|
| | | | | | Проект: Квартира с кабинетом | **М 1:25** |
| | Лист | № док. | Подпись | Дата | Шкаф распашной М_08 | |
| Дизайнер | Кырлан А.С. | | | 04.11.26 | | |

| Стадия | Лист | Листов |
|---|---|---|
| П | Д_3 | 127 |


## Вид с облицовкой

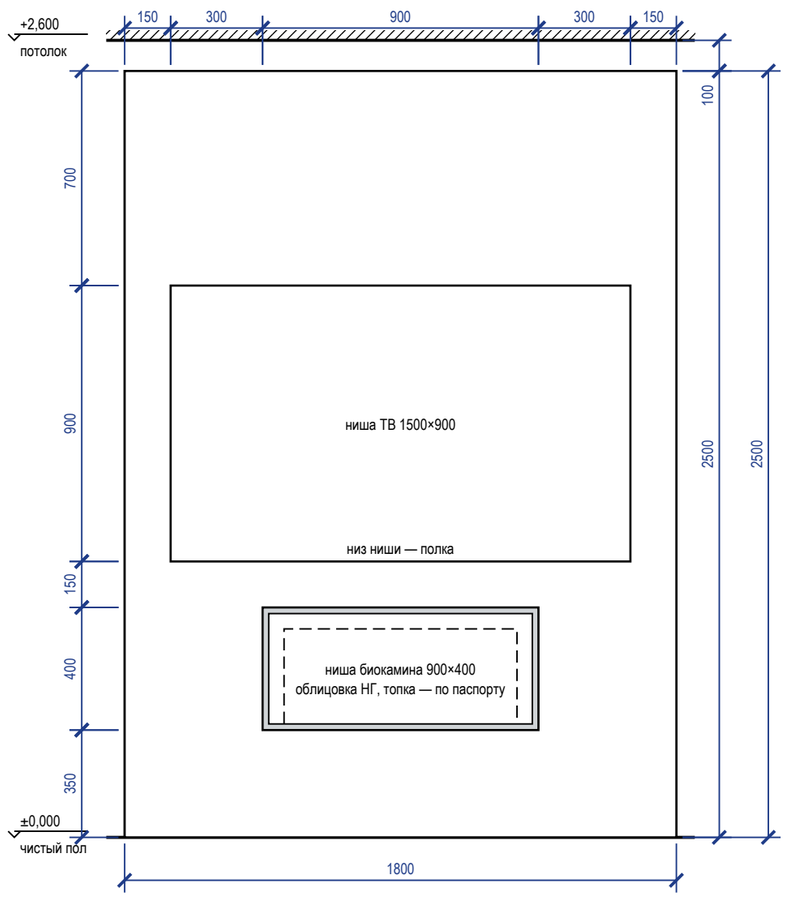


## Каркас (без облицовки)

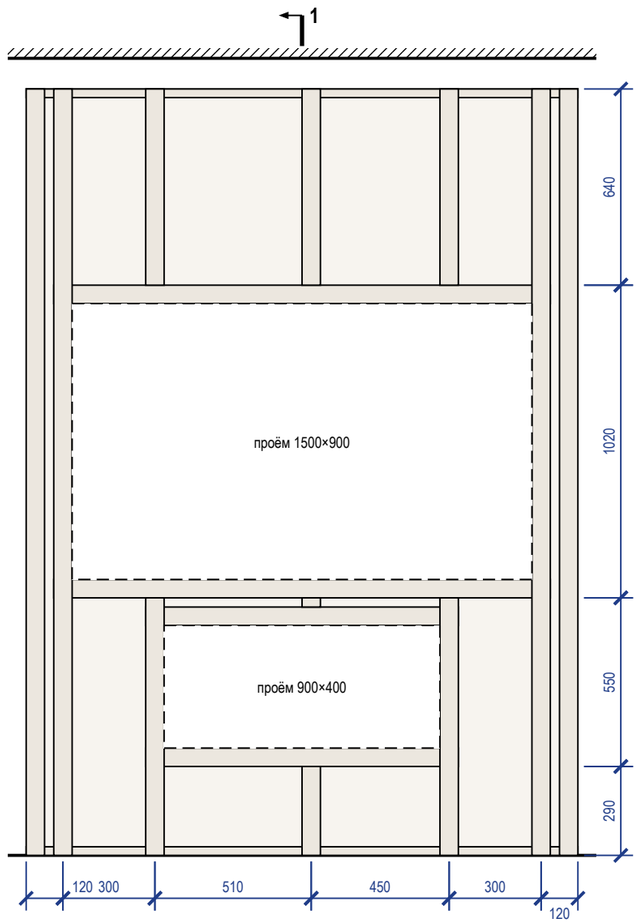



## Разрез 1-1 по нишам ТВ и биокамина

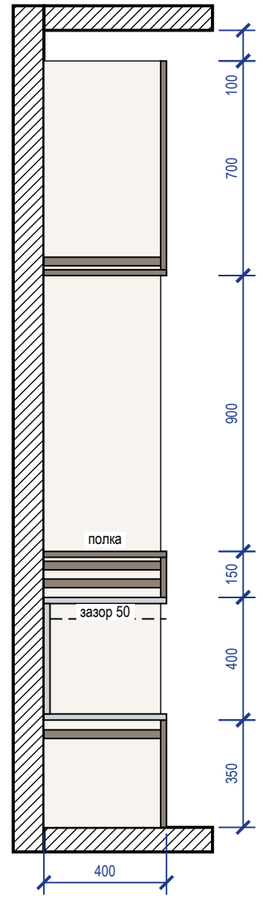


### Примечания


1. Размеры — в мм по чистовой отделке; изделие 1800×400×2500 (Ш×Г×В). Встроенная ТВ-стена, не корпусная мебель: отделений, штанг, ящиков и антресолей нет. Перед изготовлением контрольный замер стены после штукатурки и пола.
2. Каркас — оцинкованный профиль ПП 60×27 / ПН 28×27 (НГ), на стене Б; стойки по краям изделия и ниш, промежуточные с шагом не более 600 мм, ригели над и под нишами; облицовка панели МДФ 19 мм с волнистым рельефом, эмаль матовая; цвет — по колерной карте. Собирается на месте у стены, траектории подъёма нет.
3. Ниша ТВ 1500×900, низ +900, глубина 400: низ ниши — полка под приставку, электроточки ТВ-зоны — внутри ниши за телевизором, кабель-канал в каркасе.
4. Ниша биокамина 900×400, низ +350: облицовка — сталь листовая 2 мм / камень натуральный, негорючие (НГ, ГОСТ 30244), 20 мм; зазоры до топки над ней 50 мм, по бокам 50 мм — до выбора модели; окончательно — по паспорту биокамина. Каркас вокруг ниши — металлический профиль (НГ), ЛДСП, МДФ и дерево в нише и в зазорах не применять.
5. ТВ над топкой: от верха ниши биокамина (+750) до низа ниши ТВ (+900) — 150 мм; нагрев телевизора и приставки над топкой — расстояние по паспортам обеих моделей; до выбора моделей нишу ТВ не изготавливать.
6. Крепление к стене: стойки и направляющие — анкерами к основанию стены; основание стены и шаг анкеров — монтажная схема.

## 3D орто

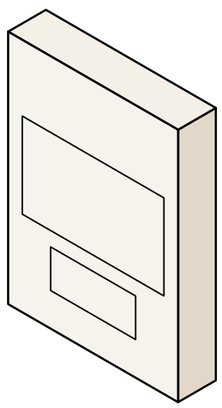


| | | | | | | |
|---|---|---|---|---|---|---|
| | | | | | Проект: Квартира с кабинетом | М 1:20 |
| | Лист | № док. | Подпись | Дата | | |
| Дизайнер | Кырлан А.С. | | | 04.11.26 | ТВ-стена M_24 | Стадия: П; Лист: Д_4; Листов: 127 |


## Вид с фасадами

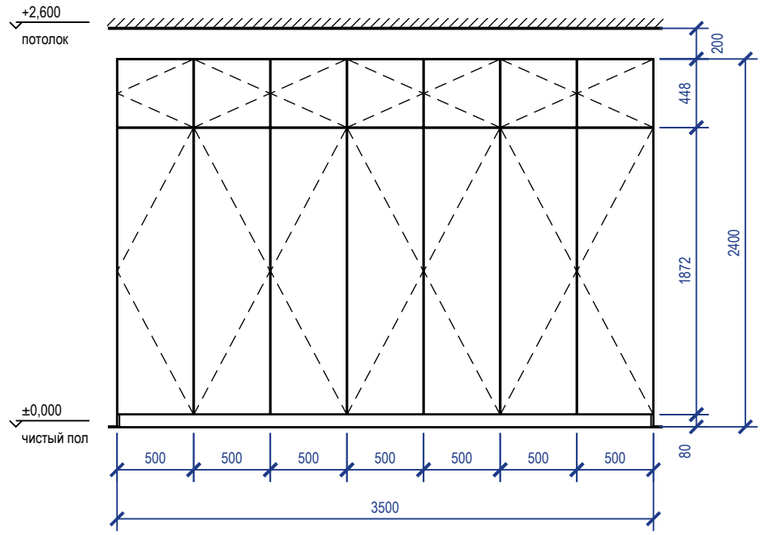



## Вид без фасадов

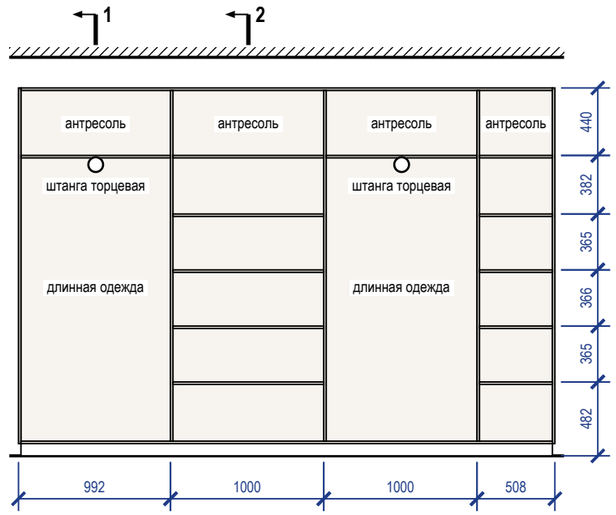


## Разрез 1-1

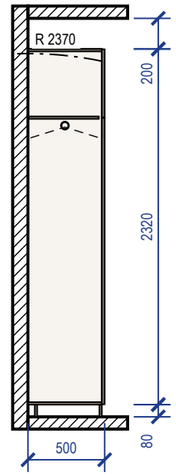


## Разрез 2-2

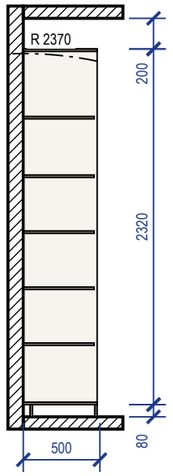


## Примечания


1. Размеры — в мм по чистовой отделке; изделие 3500×500×2400 (Ш×Г×В). Перед раскроем — контрольный замер цеха после чистовой отделки стен, пола и потолка.
2. Корпус — ЛДСП 16 мм, задняя стенка ХДФ 4 мм в паз, цоколь 80 мм на регулируемых опорах; фасады накладные — МДФ 18 мм, эмаль матовая, 18 мм; цвет — по колерной карте; петли с доводчиком: фасад 1869 мм — 4 петли, фасад 445 мм — 2 петли.
3. Кромка: скрытые торцы 0,4 мм, видимые 2 мм (ПВХ/АБС).
4. Номинальные зазоры: между фасадами 3 мм, фасад — стена и фасад — потолок не менее 3 мм, фасад ящика — стойка 2 мм.
5. Присадка по 32-й системе — выполняет цех.
6. Зазор до потолка 200 мм.
7. Подъём корпуса: диагональ боковины без цоколя √(2320² + 482²) = 2370 мм < 2600 мм до потолка — корпус собирается лёжа, поднимается поворотом и ставится на цоколь.
8. Крепление к стене от опрокидывания — уголки 2 шт. к несущему основанию (монтажная схема шкафов).

## 3D орто




| | | | | | | |
|---|---|---|---|---|---|---|
| | | | | | Проект: Квартира с кабинетом | **М 1:40** |
| | Лист | № док. | Подпись | Дата | | |
| Дизайнер | Кырлан А.С. | | | 04.11.26 | Шкаф распашной М_25 | Стадия: П; Лист: Д_5; Листов: 127 |


## Вид с фасадами

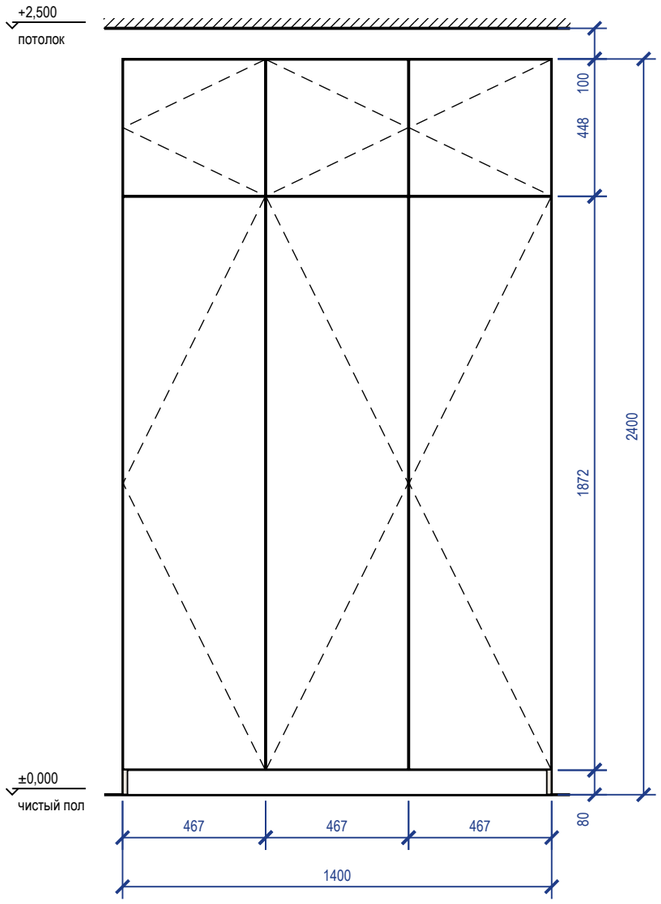



## Вид без фасадов

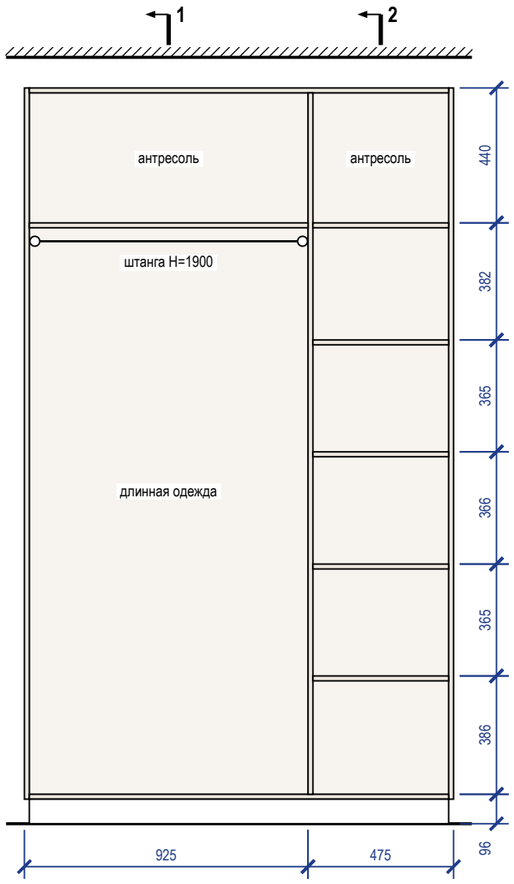


## Разрез 1-1

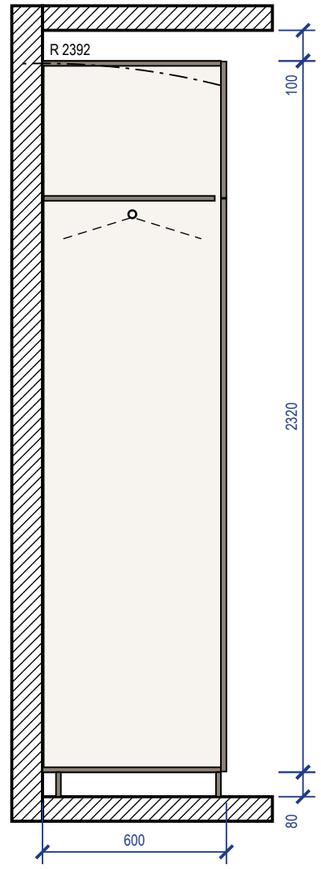



## Разрез 2-2

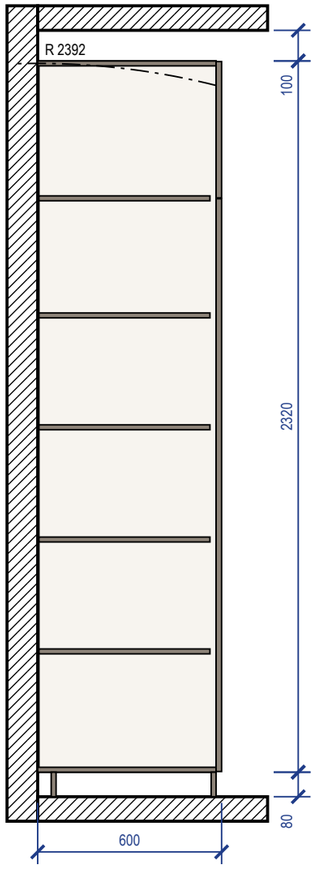


### Примечания


1. Размеры — в мм по чистовой отделке; изделие 1400×600×2400 (Ш×Г×В). Перед раскроем — контрольный замер цеха после чистовой отделки стен, пола и потолка.
2. Корпус — ЛДСП 16 мм, задняя стенка ХДФ 4 мм в паз, цоколь 80 мм на регулируемых опорах; фасады накладные — МДФ 18 мм, эмаль матовая, 18 мм; цвет — по колерной карте; петли с доводчиком: фасад 1869 мм — 4 петли, фасад 445 мм — 2 петли.
3. Кромка: скрытые торцы 0,4 мм, видимые 2 мм (ПВХ/АБС).
4. Номинальные зазоры: между фасадами 3 мм, фасад — стена и фасад — потолок не менее 3 мм, фасад ящика — стойка 2 мм.
5. Присадка по 32-й системе — выполняет цех.
6. Зазор до потолка 100 мм — закрыть планкой в цвет корпуса при монтаже.
7. Подъём корпуса: диагональ боковины без цоколя $\sqrt{(2320^2 + 582^2)} = 2392$ мм < 2500 мм до потолка — корпус собирается лёжа, поднимается поворотом и ставится на цоколь.
8. Крепление к стене от опрокидывания: крепление к стене, 2 точки; основание стены и шаг анкеров — монтажная схема шкафов.

## 3D орто

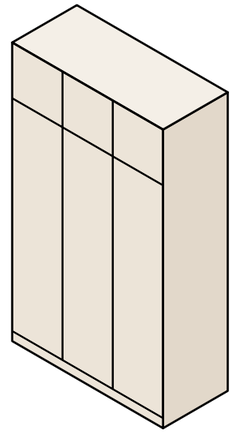


| | | | | | | |
|---|---|---|---|---|---|---|
| | | | | | Проект: Квартира с кабинетом | **М 1:20** |
| | Лист | № док. | Подпись | Дата | | |
| Дизайнер | Кырлан А.С. | | | 04.11.26 | Шкаф распашной М_26 | Стадия: П; Лист: Д_6; Листов: 127 |


## Вид с фасадами

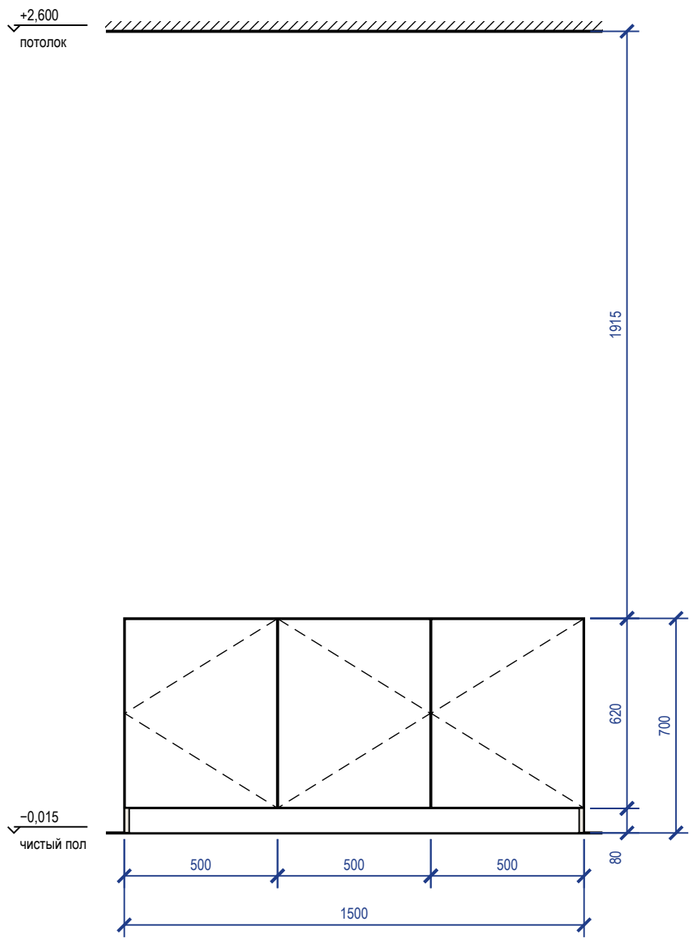


## Вид без фасадов

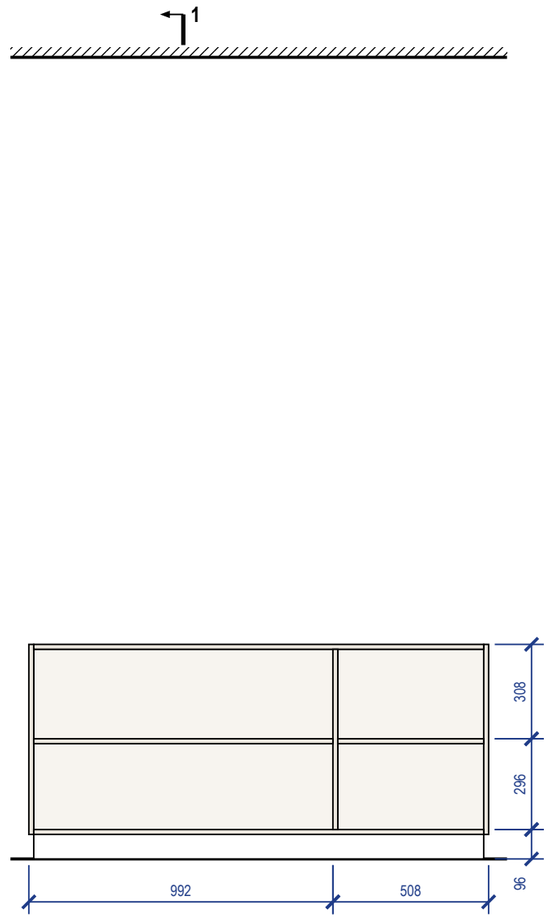



## Разрез 1-1

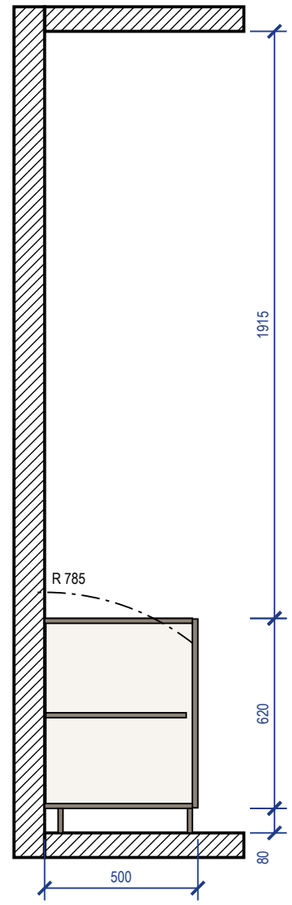


### Примечания


1. Размеры — в мм по чистовой отделке; изделие 1500×500×700 (Ш×Г×В). Перед раскроем — контрольный замер цеха после чистовой отделки стен, пола и потолка.
2. Корпус — ЛДСП 16 мм, задняя стенка ХДФ 4 мм в паз, цоколь 80 мм на регулируемых опорах; фасады накладные — МДФ 18 мм, эмаль матовая, 18 мм; цвет — по колерной карте; петли с доводчиком: фасад 616 мм — 2 петли.
3. Кромка: скрытые торцы 0,4 мм, видимые 2 мм (ПВХ/АБС).
4. Номинальные зазоры: между фасадами 3 мм, фасад — стена и фасад — потолок не менее 3 мм, фасад ящика — стойка 2 мм.
5. Присадка по 32-й системе — выполняет цех.
6. Зазор до потолка 1915 мм.
7. Подъём корпуса: диагональ боковины без цоколя √(620² + 482²) = 785 мм < 2615 мм до потолка — корпус собирается лёжа, поднимается поворотом и ставится на цоколь.
8. Крепление к стене от опрокидывания: крепление к стене, 2 точки; основание стены и шаг анкеров — монтажная схема шкафов.

## 3D орто

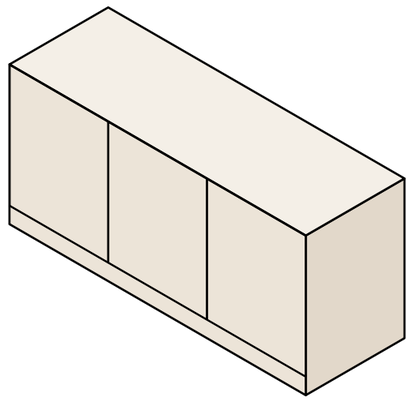


| | | | | | | |
|---|---|---|---|---|---|---|
| | | | | | Проект: Квартира с кабинетом | **М 1:20** |
| | Лист | № док. | Подпись | Дата | Тумба под раковину М_29 | Стадия / Лист / Листов |
| Дизайнер | Кырлан А.С. | | | 04.11.26 | | П / Д_7 / 127 |


## Вид с фасадами

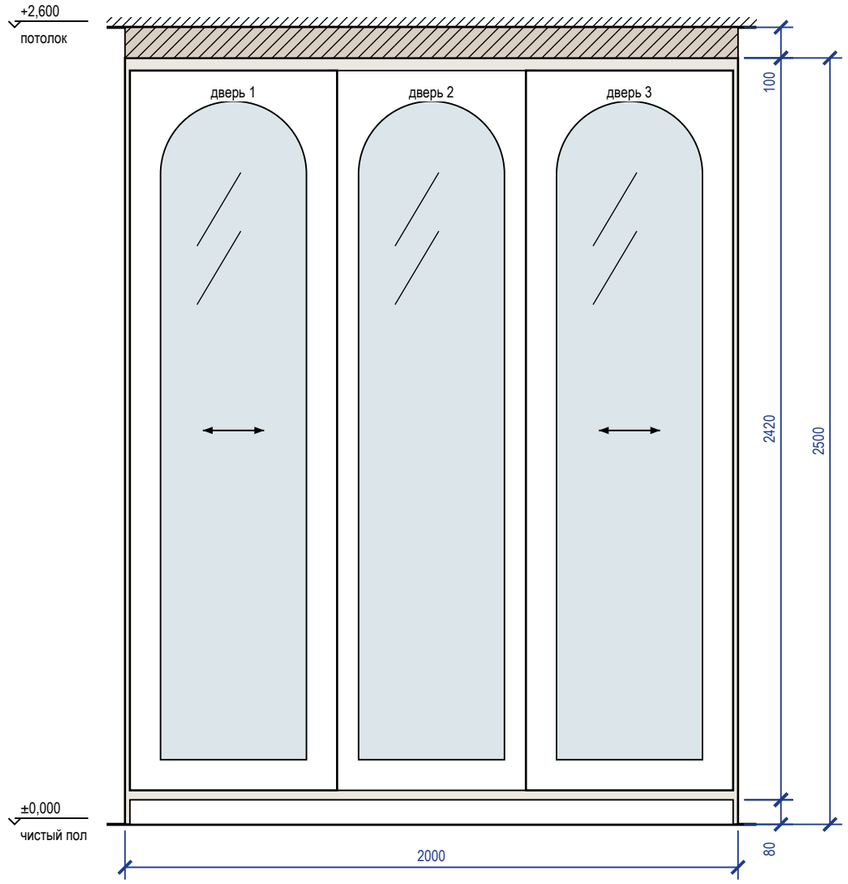



## Вид без фасадов

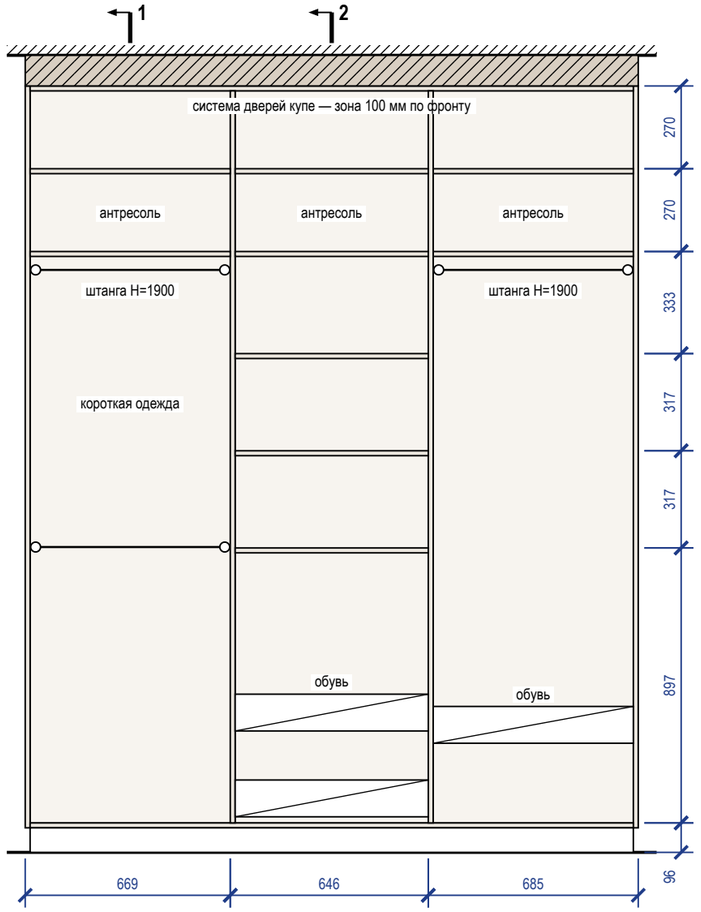


## Разрез 1-1

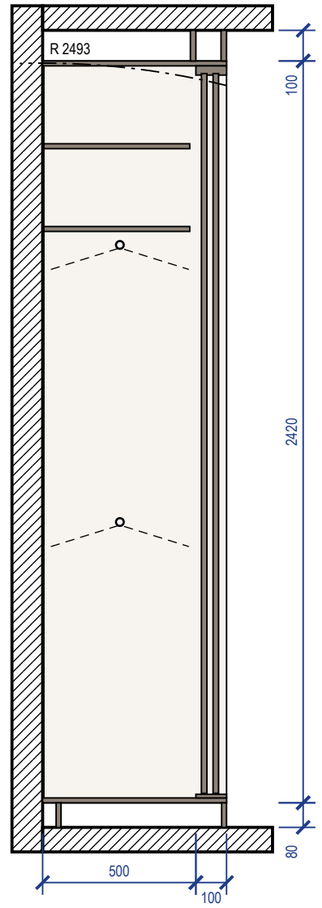



## Разрез 2-2

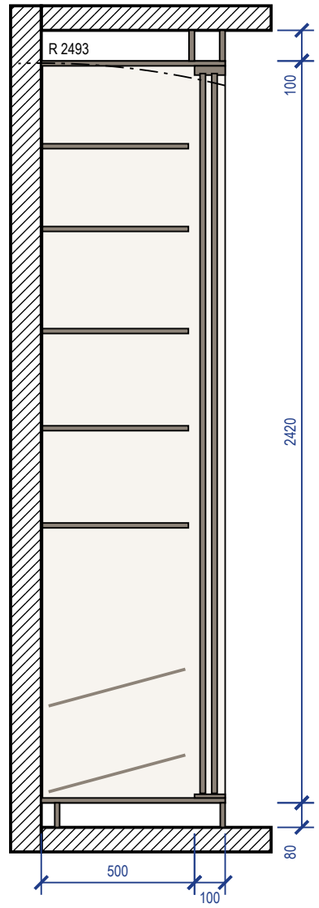


### Примечания

1. Размеры — в мм по чистовой отделке; изделие 2000×600×2500 (Ш×Г×В). Перед раскроем — контрольный замер цеха после чистовой отделки стен, пола и потолка.
2. Корпус — ЛДСП 16 мм, задняя стенка ХДФ 4 мм в паз, цоколь 80 мм на регулируемых опорах; двери купе — МДФ 10 мм, эмаль матовая в профиле: алюминий, латунь матовая; вставка зеркало серебро 4 мм, плёнка безопасности, арочная (полукруглый верх, поле 100 мм); нахлёст 30 мм, ширина двери 676 мм, высота — проём минус 40 мм; цвет — по колерной карте.
3. Кромка: скрытые торцы 0,4 мм, видимые 2 мм (ПВХ/АБС).
4. Номинальные зазоры: дверь купе — боковина 3 мм, фасад ящика — стойка 2 мм; ящики внутри купе — с накладкой 30 мм на стойке со стороны нахлёста дверей.
5. Присадка по 32-й системе — выполняет цех.
6. Компенсатор 100 мм — короб из ЛДСП по фронту и торцам, подгоняется к потолку при монтаже (припуск 20 мм), крепится к корпусу и к потолку.
7. Подъём корпуса: диагональ боковины без цоколя $\sqrt{(2420^2 + 600^2)} = 2493$ мм < 2600 мм до потолка — корпус собирается лёжа, поднимается поворотом и ставится на цоколь.
8. Крепление к стене от опрокидывания — уголки 2 шт. к несущему основанию (монтажная схема шкафов).


## 3D орто

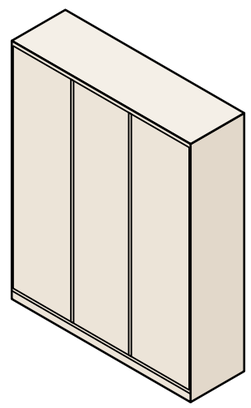


| | | | | | | | |
|---|---|---|---|---|---|---|---|
| | | | | | Проект: Квартира с кабинетом | | **M 1:20** |
| | Лист | № док. | Подпись | Дата | Шкаф-купе M_30 | Стадия | Лист | Листов |
| Дизайнер | Кырлан А.С. | | | 04.11.26 | | П | Д_8 | 127 |

выпуск 04.11.2026 № 627e1ac6ce · стр. 119 из 127


## Вид с фасадами

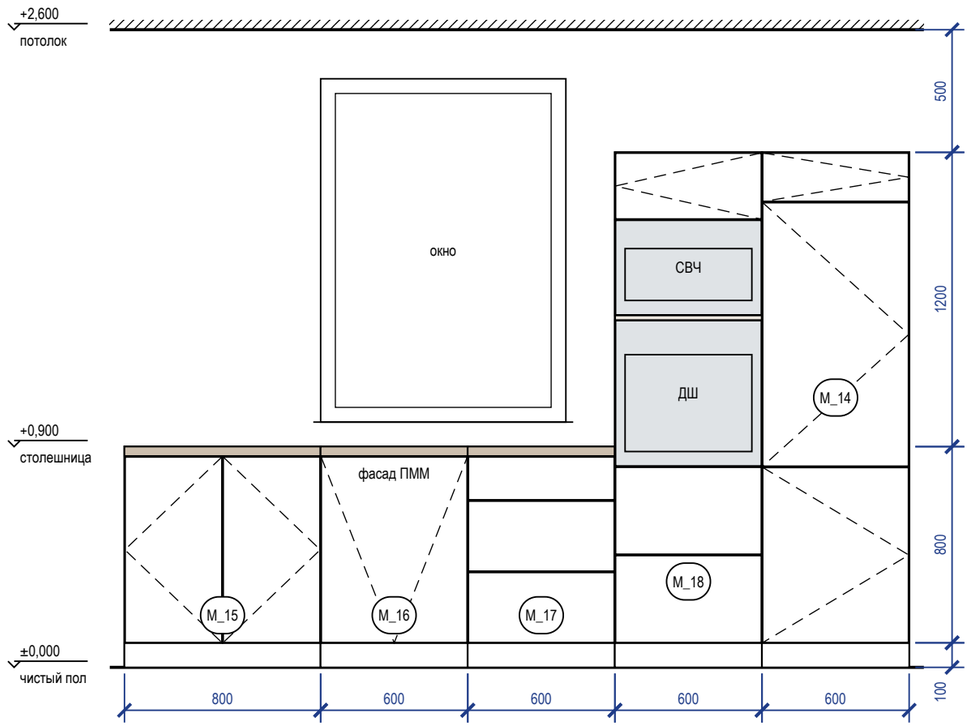



## Вид без фасадов (наполнение, выводы)

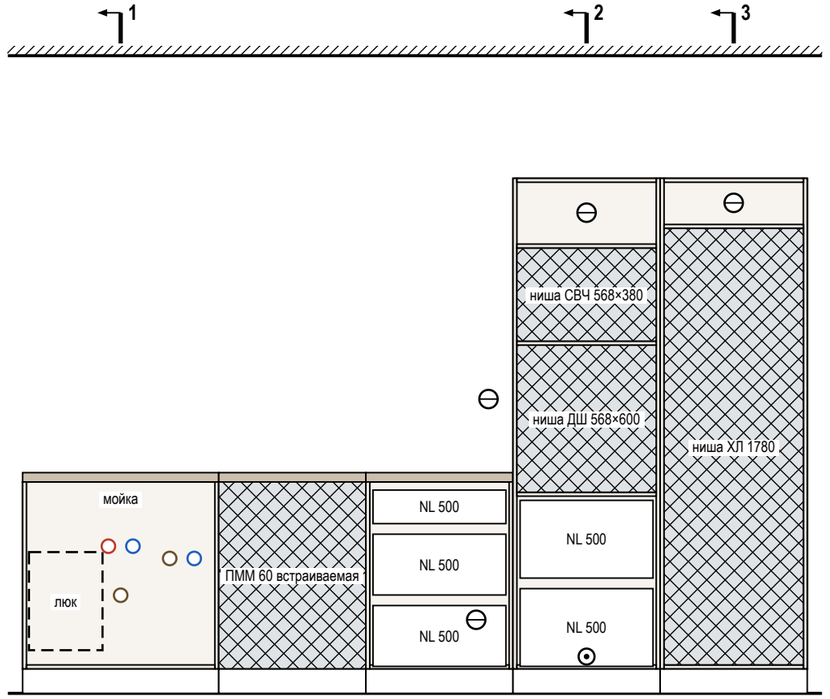



## Разрез 1-1

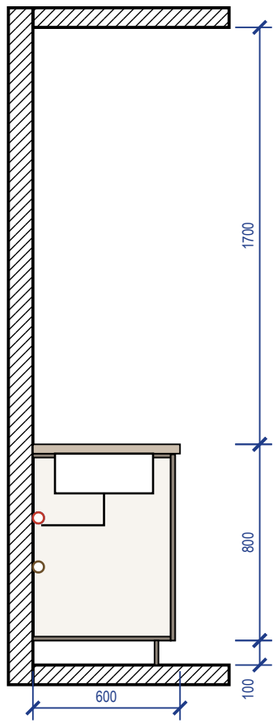



## Разрез 2-2

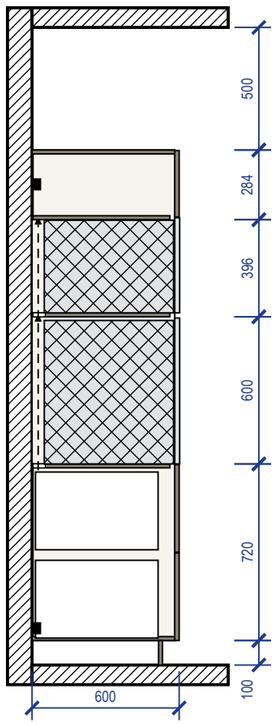


## Разрез 3-3

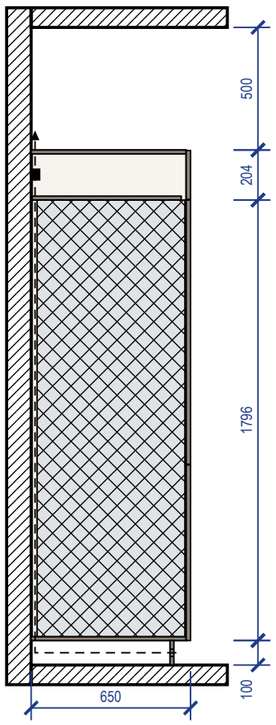


## 3D орто

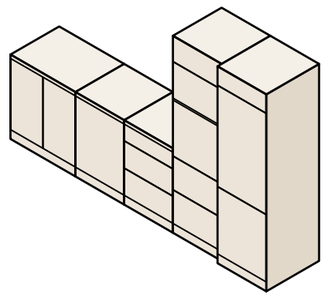


## Примечания

1. Размеры — в мм по чистовой отделке, вид из помещения; марки — как на плане расстановки. Перед раскроем — контрольный замер цеха после фартука и пола.
2. Корпуса — ЛДСП 16 мм, задняя стенка ХДФ 4 мм; фасады — МДФ, эмаль матовая 18 мм, цвет по колерной карте; столешница 38 мм, свес 20 мм; цоколь 100 мм.
3. Кромка: скрытые торцы 0,4 мм, видимые 2 мм. Номинальные зазоры: между фасадами 3 мм, фасад — столешница 3 мм, фасад — стена не менее 3 мм.
4. Ящики полного выдвижения и петли — с доводчиком; присадка по 32-й системе — выполняет цех.
5. Ниши техники (холодильник — ориентир 1780 мм) — по монтажным схемам выбранных моделей: решётка в цоколе и канал за пеналом холодильника, зазор за духовым шкафом, фасад ПММ на двери машины.
6. Вентиляция: задняя стенка в зоне ниш не ставится, зазор 50 мм до стены, щель 50 мм в полке под каждой нишей у задней стенки.
7. М_15: сервисный люк к стоякам Ст К1-3 (кухня), Ст В1-3 — съёмная панель 300×400 мм в задней стенке на саморезах (по виду без фасадов, штриховой контур «люк»), доступ через фасад модуля; короб стояков за модулем — с ревизией напротив люка (лист ВК).


| | | | | | | |
|---|---|---|---|---|---|---|
| | | | | | Проект: Квартира с кабинетом | М 1:25 |
| | Лист | № док. | Подпись | Дата | Кухня (пом. 4). Развёртка гарнитура | Стадия / Лист / Листов |
| Дизайнер | Кырлан А.С. | | | 04.11.26 | | П / Д_9 / 127 |

## План (вид сверху)

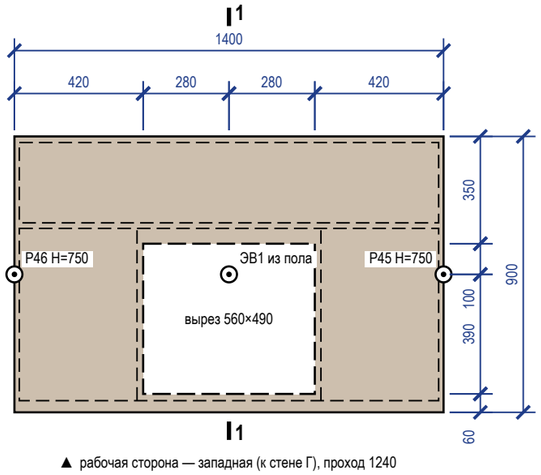



▲ рабочая сторона — западная (к стене Г), проход 1240


## Вид с рабочей стороны

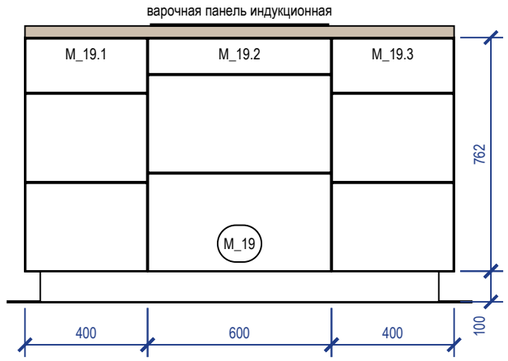


## Вид без фасадов (наполнение, вывод)

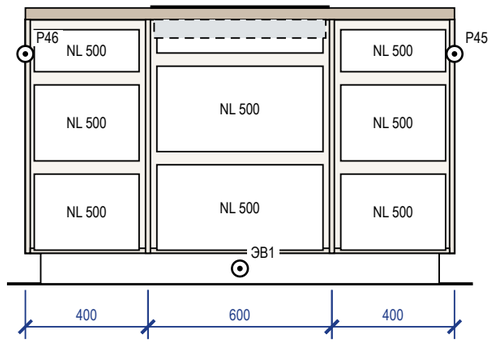


## Разрез 1-1 через варочную

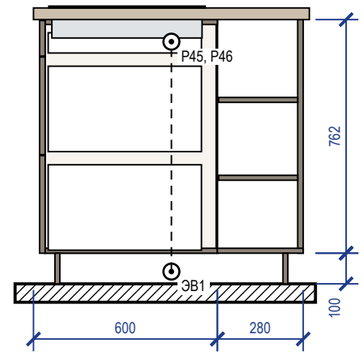


## 3D орто



## Примечания

1. Размеры — в мм по чистовому полу; перед раскроем — контрольный замер цеха после укладки пола. Остров крепится к полу (уголки в цоколе), выравнивается опорами ±20 мм.
2. Корпуса — ЛДСП 16 мм, задняя стенка ХДФ 4 мм; фасады — МДФ, эмаль матовая 18 мм; столешница 38 мм (материал — по наименованию изделия: столешница травертин), свес 20 мм по периметру; цоколь 100 мм с отступом 50 мм.
3. Кромка: скрытые торцы 0,4 мм, видимые 2 мм. Номинальные зазоры: между фасадами 3 мм, фасад — столешница 3 мм.
4. Рабочая сторона — западная (к стене Г): проход 1240 мм; с тыла — открытые полки глубиной 262 мм. Членение и сторона — предложение мебельщика.
5. Варочная панель индукционная 60 см: вырез 560×490, передняя кромка выреза в 60 мм от рабочего края; верхний ящик под панелью — с зазором 40 мм под корпус панели (вентиляция индукции); размеры выреза — по шаблону выбранной модели.
6. Питание: ЭВ1 — варочная панель на острове — вывод из пола под островом, в цоколе; P45 — столешница острова — в торцевой панели, H=750; P46 столешница острова — в торцевой панели, H=750; кабель — внутри модуля до панели, доступ через съёмный цоколь.
7. Вытяжка над островом — островная потолочная, режим рециркуляции (угольный фильтр), ширина 900, низ +1550; низ — не ниже 650 мм над панелью или по паспорту модели.

## Спецификация изделия M_19

| Поз. | Наименование | Тип, размер | Кол. |
|---|---|---|---|
| M_19.1 | модуль с ящиками | 400×900×900 | 1 |
| M_19.2 | модуль под варочную панель | 600×900×900 | 1 |
| M_19.3 | модуль с ящиками | 400×900×900 | 1 |
| M_19.2 | Варочная панель индукционная, 60 см | вырез 560 × 490, кромка выреза в 60 от рабочего края | 1 |
| | Направляющие полного выдвижения с доводчиком NL 500 | пара | 9 |
| | Ручка-профиль | латунь матовая | 9 |
| | Опора кухонная регулируемая 100–120 мм | + клипса цоколя | 12 |
| | Уголок крепления острова к полу | стальной, в цоколе | 4 |
| | Полкодержатель с фиксацией | ø5 мм | 24 |

| | | | | | | |
|---|---|---|---|---|---|---|
| | | | | | Проект: Квартира с кабинетом | **M 1:20** |
| | Лист | № док. | Подпись | Дата | | |
| Дизайнер | Кырлан А.С. | | | 04.11.26 | Остров M_19 (пом. 4). Чертёж изделия | Стадия: П; Лист: Д_10; Листов: 127 |

## Ведомость отделки помещений (форма 1 прил. А ГОСТ 21.501-2018). Лист 1 из 2

| № | Наименование помещения | Потолок | | | Стены и перегородки | | | Низ стен (плинтус) | | | Пол | | Примечание |
|---|---|---|---|---|---|---|---|---|---|---|---|---|---|
| | | Вид отделки | Код цвета | S, м² | Вид отделки | Код цвета | S, м² | Вид отделки | Код цвета | L, м | Вид отделки | S, м² | |
| 1 | Спальня<br>17,89 м² | ГКЛ по каркасу П113, отм. +2,500; +2,600; окраска, Tikkurila Anti-Reflex 2, глубокоматовая, 2 слоя, подготовка Q3 | Tikkurila V503 | 17,89 | Окраска, Farrow & Ball Modern Emulsion, матовая, 2 слоя, подготовка Q3<br><br>Акцент — стена А: окраска, Farrow & Ball Modern Emulsion, матовая, 2 слоя, подготовка Q3 | Farrow & Ball No. 15<br><br>Farrow & Ball No. 34 | 29,37<br><br>6,55 | Плинтус МДФ h=80 мм, аналог: МДФ под покраску 80×16 | Farrow & Ball No. 15 | 16,2 | Инженерная доска, 1167-4250, 2100×127 мм, на клею; тип 1, отм. ЧП ±0,000 | 17,89 | Н стен 2500 (до потолка); плинтус в цвет: стены |
| 2 | Гардеробная-постирочная<br>5,11 м² | Существующий потолок, отм. +2,700; окраска, Tikkurila Anti-Reflex 2, глубокоматовая, 2 слоя, подготовка Q3 | Tikkurila V503 | 5,11 | Окраска, Tikkurila Harmony, матовая, 2 слоя, подготовка Q3 | Tikkurila V503 | 22,94 | Плинтус МДФ h=80 мм, аналог: МДФ под покраску 80×16 | Tikkurila V503 | 8,3 | Инженерная доска, 1167-4250, 2100×127 мм, на клею; тип 1, отм. ЧП ±0,000 | 5,11 | Н стен 2700 (до потолка); плинтус в цвет: стены |
| 3 | Кабинет<br>18,92 м² | ГКЛ по каркасу П113, отм. +2,500; +2,600; окраска, Tikkurila Anti-Reflex 2, глубокоматовая, 2 слоя, подготовка Q3 | Tikkurila V503 | 18,92 | Окраска, Farrow & Ball Modern Emulsion, матовая, 2 слоя, подготовка Q3<br><br>Акцент — стена А: окраска, Farrow & Ball Modern Emulsion, матовая, 2 слоя, подготовка Q3 | Farrow & Ball No. 15<br><br>Farrow & Ball No. 34 | 33,01<br><br>5,04 | Плинтус МДФ h=80 мм, аналог: МДФ под покраску 80×16 | Farrow & Ball No. 15 | 16,7 | Инженерная доска, 1167-4250, 2100×127 мм, на клею; тип 1, отм. ЧП ±0,000 | 18,92 | Н стен 2500 (до потолка); плинтус в цвет: стены |
| 4 | Кухня-гостиная<br>45,51 м² | ГКЛ по каркасу П113, отм. +2,600; +2,500; окраска, Tikkurila Anti-Reflex 2, глубокоматовая, 2 слоя, подготовка Q3 | Tikkurila V503 | 45,51 | Окраска, Farrow & Ball Modern Emulsion, матовая, 2 слоя, подготовка Q3<br><br>Акцент — стена А: окраска, Farrow & Ball Modern Emulsion, матовая, 2 слоя, подготовка Q3<br>Фартук кухни (стена А): облицовка керамогранитом, аналог: керамогранит под травертин, матовый, 1200×600×9 мм, клей C2 TE S1, затирка CG2WA | Farrow & Ball No. 15<br><br>Farrow & Ball No. 34<br><br>по артикулу | 46,70<br><br>14,92<br><br>0,70 | Плинтус МДФ h=80 мм, аналог: МДФ под покраску 80×16 | Farrow & Ball No. 15 | 25,9 | Инженерная доска, 1167-4250, 2100×127 мм, на клею; тип 1, отм. ЧП ±0,000 | 45,51 | Н стен 2600 (до потолка); матовая моющаяся, класс 1 EN 13300 — осознанно вместо полуматовой; плинтус в цвет: стены |
| 5 | Коридор<br>9,07 м² | ГКЛ по каркасу П113, отм. +2,600; окраска, Tikkurila Anti-Reflex 2, глубокоматовая, 2 слоя, подготовка Q3 | Tikkurila V503 | 9,07 | Окраска, Farrow & Ball Modern Emulsion, матовая, 2 слоя, подготовка Q3 | Farrow & Ball No. 15 | 31,82 | Плинтус МДФ h=80 мм, аналог: МДФ под покраску 80×16 | Farrow & Ball No. 15 | 11,2 | Инженерная доска, 1167-4250, 2100×127 мм, на клею; тип 1, отм. ЧП ±0,000 | 9,07 | Н стен 2600 (до потолка); матовая моющаяся, класс 1 EN 13300 — осознанно вместо полуматовой; плинтус в цвет: стены |
| 6 | Детская<br>9,97 м² | ГКЛ по каркасу П113, отм. +2,500; +2,600; окраска, Tikkurila Anti-Reflex 2, глубокоматовая, 2 слоя, подготовка Q3 | Tikkurila V503 | 9,97 | Окраска, Farrow & Ball Modern Emulsion, матовая, 2 слоя, подготовка Q3<br><br>Акцент — стена А: окраска, Farrow & Ball Modern Emulsion, матовая, 2 слоя, подготовка Q3 | Farrow & Ball No. 15<br><br>Farrow & Ball No. 34 | 18,48<br><br>7,42 | Плинтус МДФ h=69 мм, SX165 | Farrow & Ball No. 15 | 12,0 | Инженерная доска, 1167-4250, 2100×127 мм, на клею; тип 1, отм. ЧП ±0,000 | 9,97 | Н стен 2500 (до потолка); плинтус в цвет: стены |
| 7 | Ванная<br>8,44 м² | ГКЛВ по каркасу П113, отм. +2,600; окраска, Tikkurila Luja 7, матовая, 2 слоя, подготовка Q3 | Tikkurila V503 | 8,44 | Облицовка плиткой, A8UZ, 600×1200×9 мм, клей C2 TE S1, затирка CG2WA | Atlas Concorde A8UZ | 28,76 | нет | | | Аналог: керамогранит ректифицированный под травертин, матовый, 600×600×9 мм; тип 2, отм. ЧП −0,015 | 8,44 | Н стен 2615 (до потолка); гидроизоляция обмазочная, 2 слоя, с заведением на стены 200 мм; над ванной — до 2000 и 300 мм за борт (по пирогу пола); тест проливом и акт скрытых работ |
| 8 | Прихожая<br>7,89 м² | ГКЛ по каркасу П113, отм. +2,600; окраска, Tikkurila Anti-Reflex 2, глубокоматовая, 2 слоя, подготовка Q3 | Tikkurila V503 | 7,89 | Окраска, Farrow & Ball Modern Emulsion, матовая, 2 слоя, подготовка Q3 | Farrow & Ball No. 15 | 20,40 | Плинтус МДФ h=80 мм, аналог: МДФ под покраску 80×16 | Farrow & Ball No. 15 | 7,0 | Керамогранит, A8UZ, 600×1200×9 мм; тип 3, отм. ЧП ±0,000 | 7,89 | Н стен 2600 (до потолка); матовая моющаяся, класс 1 EN 13300 — осознанно вместо полуматовой; плинтус в цвет: стены |
| 9 | Санузел гостевой<br>4,49 м² | ГКЛВ по каркасу П113, отм. +2,600; окраска, Tikkurila Luja 7, матовая, 2 слоя, подготовка Q3 | Tikkurila V503 | 4,49 | Облицовка плиткой, A8UZ, 600×1200×9 мм, клей C2 TE S1, затирка CG2WA | Atlas Concorde A8UZ | 21,44 | нет | | | Аналог: керамогранит ректифицированный под травертин, матовый, 600×600×9 мм; тип 2, отм. ЧП −0,015 | 4,49 | Н стен 2615 (до потолка); гидроизоляция обмазочная, 2 слоя, по всему помещению, с заведением на стены 200 мм; у душа — на всю высоту стен душевой зоны и 500 мм за край душевой зоны (по пирогу пола); тест проливом и акт скрытых работ |

### Примечания

1. Ведомость продолжена на листе 2 из 2; итоги, сводка площадей и примечания — на последнем листе ведомости.

| | | | | | |
|---|---|---|---|---|---|
| | | | | | Проект: Квартира с кабинетом |
| | Лист | № док. | Подпись | Дата | |
| Дизайнер | Кырлан А.С. | | | 04.11.26 | Ведомость отделки помещений. Лист 1 из 2 |

| Стадия | Лист | Листов |
|---|---|---|
| П | С1 | 127 |

## Ведомость отделки помещений (форма 1 прил. А ГОСТ 21.501-2018). Лист 2 из 2

| № | Наименование помещения | Потолок | | | Стены и перегородки | | | Низ стен (плинтус) | | | Пол | | Примечание |
|---|---|---|---|---|---|---|---|---|---|---|---|---|---|
| | | Вид отделки | Код цвета | S, м² | Вид отделки | Код цвета | S, м² | Вид отделки | Код цвета | L, м | Вид отделки | S, м² | |
| | **Итого** | | | **127,29** | | | **287,56** | | | **97,3** | | **127,29** | |

## Сводка площадей по материалам отделки

| Поверхность | Материал / код цвета | Серия | Площадь, м² |
|---|---|---|---|
| Потолок | Tikkurila V503 | Anti-Reflex 2 | 114,36 |
| Потолок | Tikkurila V503 | Luja 7 | 12,93 |
| Стены | Farrow & Ball No. 15 | Modern Emulsion | 179,79 |
| Стены | Farrow & Ball No. 34 | Modern Emulsion | 33,93 |
| Стены | Tikkurila V503 | Harmony | 22,94 |
| Стены | облицовка плиткой 600×1200×9 мм, Atlas Concorde A8UZ | A8UZ | 50,20 |
| Фартук | облицовка керамогранитом 1200×600×9 мм | аналог: керамогранит под травертин, матовый | 0,70 |

## Примечания

1. Площади поверхностей — по чистым граням стен до отделки: стены = периметр × высоту от чистого пола помещения до низа потолка минус проёмы (облицовка плиткой — до верха облицовки); плинтус = периметр минус дверные проёмы; пол и потолок — по площади помещения. Количество плиток по раскладке. Площади помещений — с учётом всех частей помещения; откосы в площадь стен не входят.
2. Акцентные стены и фартук — отдельными строками, их площадь вычтена из основной отделки стен помещения; фартук — над нижними модулями кухни от столешницы до низа навесных шкафов, где шкафов нет — на 600 мм.
3. Плинтус — длина по периметру за вычетом дверных проёмов; примыкания к наличникам и встроенной мебели — по развёрткам.
4. Формат плитки — Ш×В×Т (ширина × высота в положении укладки × толщина), мм; на полу — вдоль стен А/В × вдоль стен Б/Г.
5. Коды цвета — по веерам производителей; колеровка каждой краски одной партией, проверка выкраса при свете D65 и при лампах проекта.
6. Уровни подготовки Q1–Q4 — система Knauf, не норма ГОСТ/СП; допуски поверхностей — по СП 71.13330.2017 (действующая редакция).
7. «аналог:» — изделие задано характеристиками, марку и артикул согласовать с заказчиком до закупки.

| | | | | | | | |
|---|---|---|---|---|---|---|---|
| | | | | | Проект: Квартира с кабинетом | | |
| | Лист | № док. | Подпись | Дата | Ведомость отделки помещений. Лист 2 из 2 | Стадия | Лист | Листов |
| Дизайнер | Кырлан А.С. | | | 04.11.26 | | П | С2 | 127 |

| Поз. | Наименование и техническая характеристика | Тип, марка, обозначение документа | Код продукции | Поставщик | Ед. изм. | Кол. | Образец | Примечание |
|---|---|---|---|---|---|---|---|---|
| | **Лакокрасочные материалы** | | | | | | | |
| 1 | Краска интерьерная водно-дисперсионная акриловая для стен, матовая, класс мокрого истирания 1 по EN 13300, база A; цвет по вееру Farrow & Ball No. 15 «Bone — мягкий каменно-серый с зеленцой», колеровка машинная | Farrow & Ball Modern Emulsion | | Farrow & Ball | л | 50 | | поз. К1 колерной карты; пом. 1, 3, 4, 5, 6, 8; S = 179,8 м² × 2 сл. × 0,12 л/м² = 43,1 л, +10 % и 0,5 л на подкраску → ≥ 48,0 л; тара 10 × 5 л |
| 2 | Краска интерьерная водно-дисперсионная акриловая для акцентных стен, матовая, класс мокрого истирания 1 по EN 13300, база C; цвет по вееру Farrow & Ball No. 34 «Calke Green — традиционный шалфей», колеровка машинная | Farrow & Ball Modern Emulsion | | Farrow & Ball | л | 10 | | поз. К2 колерной карты; пом. 1, 3, 4, 6; S = 33,9 м² × 2 сл. × 0,12 л/м² = 8,1 л, +10 % и 0,5 л на подкраску → ≥ 9,5 л; тара 2 × 5 л |
| 3 | Краска интерьерная водно-дисперсионная акриловая для потолков, глубокоматовая, класс мокрого истирания 2 по EN 13300, база A; цвет по вееру Tikkurila V503 «Winter», колеровка машинная | Tikkurila Anti-Reflex 2 | | Tikkurila | л | 31,5 | | поз. К3 колерной карты; пом. 1, 2, 3, 4, 5, 6, 8; S = 114,4 м² × 2 сл. × 0,12 л/м² = 27,4 л, +10 % и 0,5 л на подкраску → ≥ 30,7 л; тара 3 × 9 л + 1 × 2,7 л + 2 × 0,9 л |
| 4 | Краска интерьерная водно-дисперсионная акриловая для стен, матовая, класс мокрого истирания 1 по EN 13300, база A; цвет по вееру Tikkurila V503 «Winter», колеровка машинная | Tikkurila Harmony | | Tikkurila | л | 7,2 | | поз. К5 колерной карты; пом. 2; S = 22,9 м² × 2 сл. × 0,12 л/м² = 5,5 л, +10 % и 0,5 л на подкраску → ≥ 6,6 л; тара 2 × 2,7 л + 2 × 0,9 л |
| 5 | Краска интерьерная водно-дисперсионная акриловая для потолков, матовая, класс мокрого истирания 1 по EN 13300, база A; цвет по вееру Tikkurila V503 «Winter», колеровка машинная | Tikkurila Luja 7 | | Tikkurila | л | 4,5 | | поз. К8 колерной карты; пом. 7, 9; S = 12,9 м² × 2 сл. × 0,12 л/м² = 3,1 л, +10 % и 0,5 л на подкраску → ≥ 3,9 л; тара 1 × 2,7 л + 2 × 0,9 л |
| 6 | Краска для МДФ и дерева в цвет Farrow & Ball No. 15 «Bone — мягкий каменно-серый с зеленцой» — окраска плинтуса; блеск не ниже блеска стен | марка не задана | | | л | 2,3 | | поз. К4, К7; пом. 1, 3, 4, 5, 6, 8; L = 89,0 м, S = 8,4 м² × 2 сл. × 0,12 л/м² + 10 %; продукт подобрать в веере Farrow & Ball |
| 7 | Краска для МДФ и дерева в цвет Tikkurila V503 «Winter» — окраска плинтуса; блеск не ниже блеска стен | марка не задана | | | л | 0,5 | | поз. К6; пом. 2; L = 8,3 м, S = 0,8 м² × 2 сл. × 0,12 л/м² + 10 %; продукт подобрать в веере Tikkurila |
| 8 | Грунтовка акриловая под окраску стен и потолков — из системы производителя краски | по системе краски | | | м² | 364 | | площадь окраски стен, акцентов и потолков; 1 слой перед окраской; расход — по ТУ грунтовки |
| | **Плитка и керамогранит** | | | | | | | |
| 9 | Керамогранит под травертин, 600×600×9 мм, ректификат, водопоглощение 0,1 % (BIa), противоскольжение R10, PEI IV | аналог по характеристикам | | | м² | 18,36 | | шов 2 мм; Ванная, пол; Санузел гостевой, пол; по раскладке 46 шт (S = 12,93 м²), с запасом 51 шт |
| 10 | A8UZ, 600×1200×9 мм, ректификат, водопоглощение 0,1 % (BIa), противоскольжение R10, PEI IV | A8UZ | | Atlas Concorde | м² | 111,60 | | шов 2 мм; Ванная, стены А–Г; Ванная, короб инсталляции; Санузел гостевой, стены А–Г; Санузел гостевой, короб инсталляции; Прихожая, пол; по раскладке 137 шт (S = 59,81 м²), с запасом 155 шт |
| 11 | Керамогранит под травертин, матовый, 1200×600×9 мм, ректификат, водопоглощение 0,1 % (BIa) | аналог по характеристикам | | | м² | 2,16 | | шов 2 мм; Кухня-гостиная, фартук (ст. А); по раскладке 2 шт (S = 0,70 м²), с запасом 3 шт |
| | **Напольные покрытия** | | | | | | | |
| 12 | 1167-4250, рабочий слой 4 мм, эмиссия E1, укладка на клей | 1167-4250 | | Coswick | м² | 114 | | пом. 1, 2, 3, 4, 5, 6; S = 106,47 м² + 7 % (прямая укладка); к заказу — кратно упаковке |
| 13 | Клей для паркета и инженерной доски, эластичный (СМП / полиуретановый) | по рекомендации производителя доски | | | м² | 107 | | площадь приклейки; расход и шпатель — по ТУ клея |
| | **Погонажные изделия** | | | | | | | |
| 14 | Плинтус МДФ под покраску 80×16, крепление к стене, окраска в цвет Farrow & Ball No. 15 | аналог по характеристикам | | | м | 85 | | пом. 1, 3, 4, 5, 8; L = 77,0 м (периметр без дверных проёмов) + 10 % на подрезку; в штуках — по длине планки |
| 15 | Плинтус МДФ под покраску 80×16, крепление к стене, окраска в цвет Tikkurila V503 | аналог по характеристикам | | | м | 10 | | пом. 2; L = 8,3 м (периметр без дверных проёмов) + 10 % на подрезку; в штуках — по длине планки |
| 16 | SX165, h = 69 мм, крепление к стене, окраска в цвет Farrow & Ball No. 15 | SX165 | | Orac Decor | м | 14 | | пом. 6; L = 12,0 м (периметр без дверных проёмов) + 10 % на подрезку; в штуках — по длине планки |
| | **Смеси и материалы для облицовки** | | | | | | | |
| 17 | Затирка для швов плитки, класс CG2WA по EN 13888 | Mapei Ultracolor Plus 132 | | Mapei | кг | 6 | | по раскладке (a+b)/(a·b) × шов × t × 1,6 + 10 %; в т. ч. 0,7 кг — позиции раскладки без марки |
| 18 | Клей плиточный C2 TE S1 по EN 12004, слой 5 мм | Ceresit CM 17 | | Ceresit | кг | 590 | | 24 меш. по 25 кг; 1,5 кг/м² на 1 мм слоя + 10 %; в т. ч. 70 кг — позиции раскладки без марки |
| 19 | Гидроизоляция обмазочная мокрых зон: пол, стены по периметру, зоны замачивания; 2 слоя с армирующей лентой в углах | аналог по характеристикам | | | м² | 33 | | площадь по листу раскладки плитки + 10 %; расход смеси — по ТУ |
| 20 | Лента демпферная по периметру пола из плитки | аналог по характеристикам | | | м | 28 | | периметр без дверных проёмов + 10 % |

## Примечания

1. Количества — из геометрии проекта: площади поверхностей по чистым граням стен до отделки (те же, что в ведомости отделки и колерной карте), плитка, клей и затирка — по раскладке плиточника; в графе «Кол.» — к заказу, с запасом.
2. Краска: расход 0,12 л/м² на слой в 2 слоя, если по ТУ не задан иной; запас 10 % и 0,5 л на подкраску каждого кода. Один код — одна партия, колеровка машинная в колеровочном центре бренда; в заказ — только после утверждения выкраса (колерная карта). Фасовка — по каталогу бренда на дату выпуска; к заказу — не меньше расчётного объёма.
3. «Аналог по характеристикам» — допускается изделие другого производителя с характеристиками не ниже указанных, по согласованию с автором проекта.
4. Графы «Код продукции» и «Масса 1 ед.» не заполнены: коды по классификатору продукции не присвоены, масса единицы до 25 кг (ГОСТ 21.110-2013).
5. Грунтовка и клей для доски указаны площадью обработки; объём — по ТУ выбранного продукта.

| | | | | | |
|---|---|---|---|---|---|
| | | | | | Проект: Квартира с кабинетом |
| | Лист | № док. | Подпись | Дата | |
| Дизайнер | Кырлан А.С. | | | 04.11.26 | Спецификация отделочных материалов |

| Стадия | Лист | Листов |
|---|---|---|
| П | С3 | 127 |

## Список покупок: материалы для магазина

| № | Что купить | Артикул или характеристика | Нужно с запасом | Брать в магазине | Фасовка | Уточнить в магазине | Помещения | Кто покупает |
|---|---|---|---|---|---|---|---|---|
| **Покрытия полов и облицовка** | | | | | | | | |
| 1 | Инженерная доска (дуб натуральный, рабочий слой 4 мм, эмиссия E1, прямая укладка) | 1167-4250 | 114,54 м² | 114,6 м² | | уточнить в магазине: м² в упаковке | 1, 2, 3, 4, 5, 6 | по проекту |
| 2 | Клей для паркетной и инженерной доски (эластичный, по ТУ изготовителя доски) | на выбор бригады по проекту | 107,05 м² | | | уточнить в магазине: расход и фасовку — по выбранному продукту | | бригада |
| 3 | Керамогранит 600×600 мм под травертин | по характеристике: керамогранит под травертин | 51 шт | 51 шт | | уточнить в магазине: штук в коробке | 7, 9 | по проекту |
| 4 | Керамогранит 600×1200 мм A8UZ | A8UZ | 151 шт | 155 шт | | уточнить в магазине: штук в коробке | 7, 8, 9 | по проекту |
| 5 | Керамогранит 1200×600 мм под травертин, матовый | по характеристике: керамогранит под травертин, матовый | 3 шт | 3 шт | | уточнить в магазине: штук в коробке | 4 | по проекту |
| **Сухие смеси и гидроизоляция** | | | | | | | | |
| 6 | Клей плиточный цементный класса C2 TE S1 (ГОСТ Р 56387-2018) | Ceresit CM 17 или аналог | 589,59 кг | 24 меш. | мешок 25 кг | | | по проекту |
| 7 | Затирка цементная класса CG2WA, цвет — по колерной карте | Mapei Ultracolor Plus 132 или аналог | 5,98 кг | 3 упак. | упак. 2 кг | | | по проекту |
| 8 | Гидроизоляция обмазочная полимерная, 2 слоя, лента в углах, манжеты на выводах | на выбор бригады по проекту | 33,02 м² | | | уточнить в магазине: расход и фасовку — по выбранному продукту | 7, 9 | бригада |
| 9 | Лента демпферная по периметру пола из плитки | на выбор бригады по проекту | 27,98 м | 28 м | | уточнить в магазине: фасовку | | бригада |
| 10 | Смесь цементно-песчаная для стяжки М200 (50 мм, 33 мм) | на выбор бригады по проекту | 6,5 м³ | | | уточнить в магазине: расход и фасовку — по выбранному продукту | | бригада |
| 11 | Смесь штукатурная гипсовая для машинного и ручного нанесения по маякам, слой до 10 мм | на выбор бригады по проекту | 316,32 м² | | | уточнить в магазине: расход и фасовку — по выбранному продукту | 1, 2, 3, 4, 5, 6, 7, 8, 9 | бригада |
| **Короба из ГКЛВ** | | | | | | | | |
| 12 | Лист ГКЛВ 12,5 мм, 2500 × 1200 мм, обшивка коробов в 2 слоя | на выбор бригады по проекту | 9,35 м² | 4 лист. | лист 3,00 м² | | 7, 9 | бригада |
| 13 | Профиль стальной оцинкованный 27 × 28 мм: каркас коробов (стойки и направляющие) | на выбор бригады по проекту | 20,02 м | 7 шт | хлыст 3 м | | | бригада |
| **Слаботочные сети** | | | | | | | | |
| 14 | Кабель домофона — тип по системе поставщика | на выбор бригады по проекту | 5,7 м | 6 м | | уточнить в магазине: длину бухты | | бригада |
| 15 | Кабель коаксиальный RG-6 (75 Ом) к розеткам ТВ | на выбор бригады по проекту | 57 м | 57 м | | уточнить в магазине: длину бухты | | бригада |
| 16 | Кабель U/UTP кат. 6 (LAN, Wi-Fi и камеры по PoE) | на выбор бригады по проекту | 110,6 м | 111 м | | уточнить в магазине: длину бухты | | бригада |
| 17 | Гофротруба Ø20 для слаботочных линий, отдельно от силовых | на выбор бригады по проекту | 156 м | 156 м | | уточнить в магазине: длину бухты | | бригада |
| 18 | Розетка компьютерная RJ45, кат. 6, с рамкой и подрозетником | на выбор бригады по проекту | 5 шт | 5 шт | шт | | | бригада |
| 19 | Розетка телевизионная (коаксиальная) с рамкой и подрозетником | на выбор бригады по проекту | 3 шт | 3 шт | шт | | | бригада |

| | | | | | |
|---|---|---|---|---|---|
| | | | | | Проект: Квартира с кабинетом |
| | Лист | № док. | Подпись | Дата | Список покупок |
| Дизайнер | Кырлан А.С. | | | 04.11.26 | |

| Стадия | Лист | Листов |
|---|---|---|
| П | С4 | 127 |

## Список покупок: материалы для магазина (продолжение)

| № | Что купить | Артикул или характеристика | Нужно с запасом | Брать в магазине | Фасовка | Уточнить в магазине | Помещения | Кто покупает |
|---|---|---|---|---|---|---|---|---|
| 20 | Трубка или монитор домофона (поставка домофонной организации) | на выбор бригады по проекту | 1 шт | 1 шт | шт | | | по проекту |
| 21 | Щит слаботочный ЩС: корпус, DIN-рейка, розетки 220 В | на выбор бригады по проекту | 1 шт | 1 шт | шт | | | бригада |
| 22 | Патч-панель, портов не менее 7 | на выбор бригады по проекту | 1 шт | 1 шт | шт | | | бригада |
| **Лакокрасочные материалы** | | | | | | | | |
| 23 | Краска интерьерная акриловая, матовая, класс истирания 1 | Farrow & Ball Modern Emulsion No. 34 «Calke Green — традиционный шалфей» | 8,95 л | 4 банк. | банка 2,5 л | | 1, 3, 4, 6 | по проекту |
| 24 | Краска интерьерная акриловая, матовая, класс истирания 1 | Farrow & Ball Modern Emulsion No. 15 «Bone — мягкий каменно-серый с зеленцой» | 47,47 л | 19 банк. | банка 2,5 л | | 1, 3, 4, 5, 6, 8 | по проекту |
| 25 | Краска интерьерная акриловая, глубокоматовая, класс истирания 2 | Tikkurila Anti-Reflex 2 V503 «Winter» | 30,2 л | 12 банк. | банка 2,7 л | | 1, 2, 3, 4, 5, 6, 8 | по проекту |
| 26 | Краска интерьерная акриловая, матовая, класс истирания 1 | Tikkurila Harmony V503 «Winter» | 6,06 л | 3 банк. | банка 2,7 л | | 2 | по проекту |
| 27 | Краска интерьерная акриловая, матовая, класс истирания 1 | Tikkurila Luja 7 V503 «Winter» | 3,41 л | 2 банк. | банка 2,7 л | | 7, 9 | по проекту |
| 28 | Шпаклёвка финишная полимерная под окраску (стены и потолки, Q3) | на выбор бригады по проекту | 400,35 м² | | | уточнить в магазине: расход и фасовку — по выбранному продукту | | бригада |
| 29 | Грунтовка акриловая глубокого проникновения, 2 слоя | на выбор бригады по проекту | 456,34 м² | | | уточнить в магазине: расход и фасовку — по выбранному продукту | | бригада |
| **Погонажные изделия и потолки** | | | | | | | | |
| 30 | Плинтус напольный МДФ под покраску, h=80 мм, крепление к стене | по характеристике: плинтус МДФ под покраску 80×16 | 93,92 м.п. | 40 шт | хлыст 2,4 м | | 1, 2, 3, 4, 5, 8 | по проекту |
| 31 | Плинтус напольный МДФ под покраску, h=69 мм, крепление к стене | SX165 | 13,16 м.п. | 6 шт | хлыст 2,4 м | | 6 | по проекту |
| 32 | Потолок подвесной ГКЛ/ГКЛВ по каркасу Knauf П113: листы, профили, подвесы, лента, шпаклёвка швов | Knauf П113 | 122,18 м² | | | уточнить в магазине: расход и фасовку — по выбранному продукту | | по проекту |

## Примечания

1. «Нужно с запасом» — расход по чертежам и раскладке плюс запас на подрезку и подкраску; «Брать в магазине» — то же количество в единицах, которыми продают (банки, мешки, упаковки, листы, штуки, литры).
2. «Уточнить в магазине» — фасовки этого товара в проекте нет: спросите у продавца, сколько в упаковке, и возьмите целое число упаковок не меньше «Нужно с запасом».
3. Плитку, доску и краску одного цвета берите одной партией (один калибр и тон на помещение) и сохраните чек и номер партии до конца ремонта.
4. «По характеристике» — артикул не выбран: подойдёт любой товар с этими свойствами, согласуйте его с дизайнером до покупки. «Бригада» материал выбирает и закупает бригада по своей технологии.
5. Помещения: 1 — Спальня; 2 — Гардеробная-постирочная; 3 — Кабинет; 4 — Кухня-гостиная; 5 — Коридор; 6 — Детская; 7 — Ванная; 8 — Прихожая; 9 Санузел гостевой; «—» — материал для нескольких помещений, расход по месту.




| | | | | | |
|---|---|---|---|---|---|
| | | | | | Проект: Квартира с кабинетом |
| | Лист | № док. | Подпись | Дата | |
| Дизайнер | Кырлан А.С. | | | 04.11.26 | Список покупок (окончание) |
| | | | | | |

| Стадия | Лист | Листов |
|---|---|---|
| П | С5 | 127 |


### 1 Порог 15 мм: мокрая зона — смежное помещение (М 1:10)

Применение: двери Д-6, Д-7

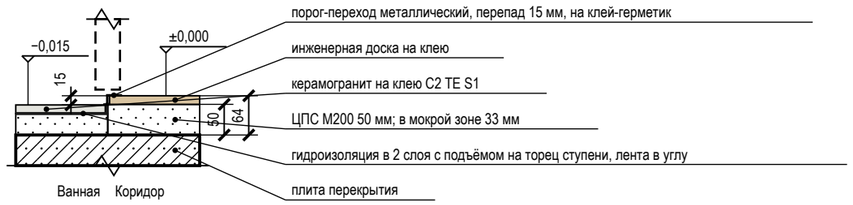



### 2 Дверь скрытого монтажа в плоскости стены, плинтус (М 1:5)

Применение: двери Д-2, Д-3, Д-4, Д-5, Д-6, Д-7

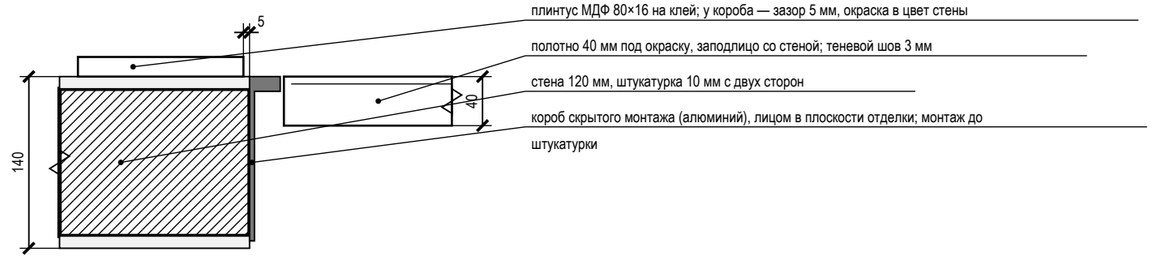



### 3 Короб стояков К1-1 с люком и звукоизоляцией (М 1:10)

Применение: пом. 9, 7, 4

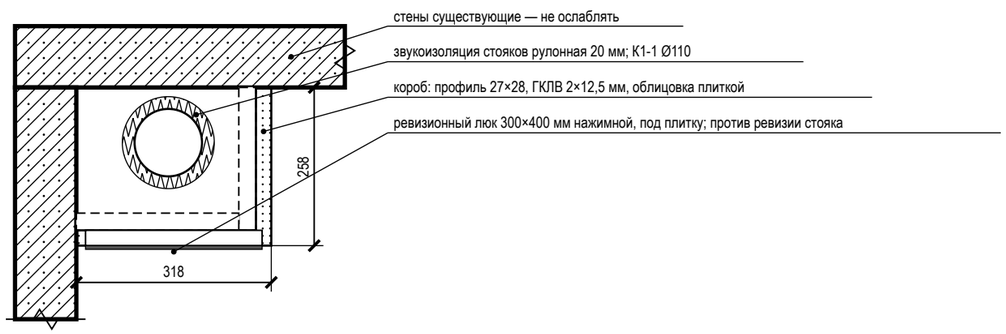



### 4 Гидроизоляция санузла: заход на стены 200 мм (М 1:20)

Применение: пом. 7, 9

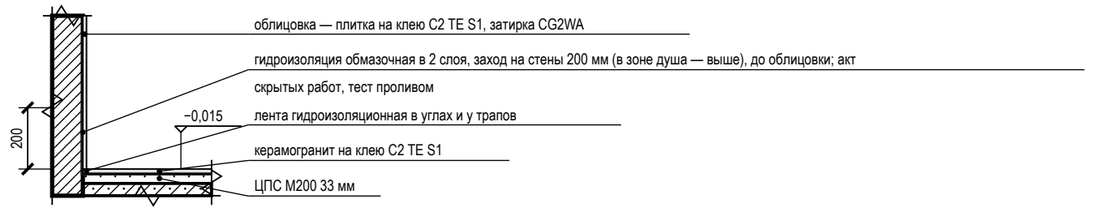



### 5 Плинтус МДФ 80×16 мм у окрашенной стены по доске (ламинату) (М 1:10)

Применение: пом. 1, 2, 3, 4, 5, 6

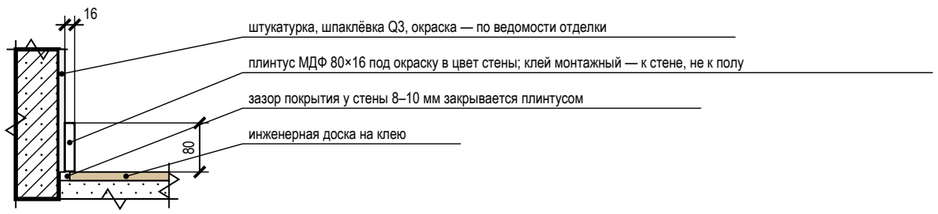


### 6 Плинтус МДФ 80×16 мм у окрашенной стены по керамограниту (плитке) (М 1:10)

Применение: пом. 8

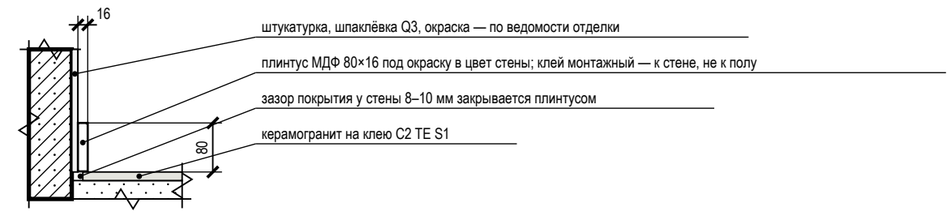


## Условные обозначения

- железобетон (плита, стены) — условно: конструкция не установлена
- кладка, перегородка — условно: конструкция не установлена
- стяжка, раствор
- гипсокартон ГКЛВ
- звукоизоляция, эластичный заполнитель
- плитка, керамогранит на клею
- инженерная доска (покрытие пола)
- металлический профиль (порог, Т-профиль, короб двери)
- гидроизоляция (обмазочная, лента)

## Примечания

1. Узлы — типовые решения проекта для мест, отмеченных выносками на листе схемы расположения развёрток и узлов; размеры — в мм, отметки — в м от ±0,000.
2. Узлы с гидроизоляцией, закладными и коробами скрытого монтажа принимаются по актам скрытых работ до закрытия отделкой; гидроизоляция — после теста проливом (24 ч).
3. Марки изделий (порог, Т-профиль, короб скрытой двери, люк) — по спецификациям; замена — на аналог с теми же габаритами по согласованию с автором проекта.
4. Материал плиты перекрытия и стен в узлах показан условно (железобетон, кладка): конструкция дома не установлена — крепёж, анкеры и толщины слоёв уточняются после обследования (до него — по допущениям общих указаний).

| | | | | | |
|---|---|---|---|---|---|
| | | | | | Проект: Квартира с кабинетом |
| | Лист | № док. | Подпись | Дата | Узлы |
| Дизайнер | Кырлан А.С. | | | 04.11.26 | |

| Стадия | Лист | Листов |
|---|---|---|
| П | С6 | 127 |