
LINEA

ДИЗАЙН-ПРОЕКТ ИНТЕРЬЕРА

Четырёхкомнатная квартира

13 помещений

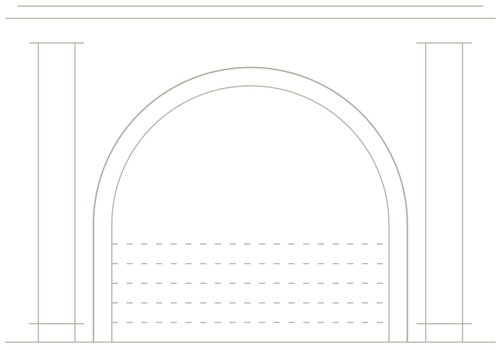


ПАЛИТРА ОТДЕЛКИ

F497	J484	L481	V486	NCS S 3005-Y20
82 %	12 %	6 %	текстиль, декор	текстиль, декор

АВТОР ПРОЕКТА

Кырлан Александр Сергеевич

Ноябрь 2026

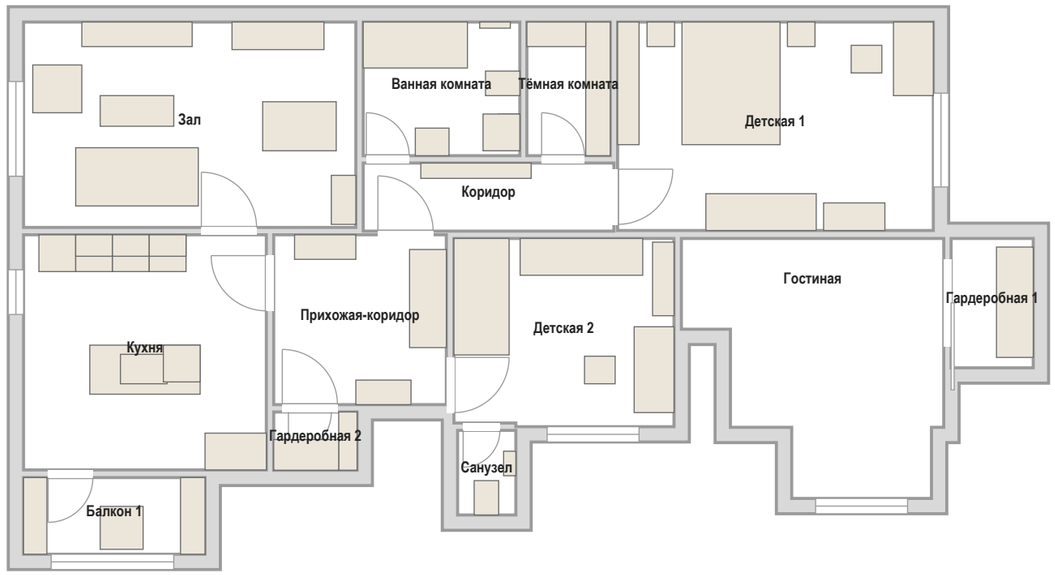

План расстановки мебели · М 1:100

ОБЩАЯ ПЛОЩАДЬ	ПОМЕЩЕНИЙ	СТАДИЯ	ШИФР	ОСНОВА
102,67 м²	13, из них жилых 4	Проект · предварительно	ГД-2026-004-АИ	план заказчика, без обмера

Как оставить правку: кнопка «Правка к этому листу» в правом верхнем углу любого листа · все листы проекта: дизайн-студия-квартир.рф/review.html?p=gost-proekt2

выпуск 04.11.2026 № 2391fcbada · стр. 1 из 120

Объект

Четырёхкомнатная квартира: 106,37 м², помещений 13, из них жилых 4.

Стиль: современный (контемпорари) 100 %. Стадия: предварительный альбом без обмера, планировка по плану заказчика.

Открытых вопросов 27, конфликтов разделов 1; изменений утверждено 13, ждут подписи 7.

Розетки и выводы

49 розеток (рамок 38), 5 выводов кабеля под технику и свет, 19 групп щита — всё с высотами от чистого пола: листы 41, 42, 43.

Что решено (подписано вами)

ИЗ-1 — Окно на наружной стене В (1580…3080.

ИЗ-2 — Добавлены: бра Св63 у изголовья кровати М_33 (стена А, смещение 510, высота 1400 мм, 6 Вт, 2700 К, линия L21) и выключатель S17 (стена А, смещение 1050, высота 900 мм).

ИЗ-3 — Добавлен светильник Св64 над зеркалом ДК17 (стена Б, смещение 600, высота 1950 мм, 8 Вт, 3000 К, IP44, драйвер встроен, линия L12, группа 4).

ИЗ-4 — В S2 добавлен светорегулятор (тип ТЕ, под диммируемую ленту).

ИЗ-6 — Полотно раздвижное, две створки по 710 мм по накладной направляющей.

ИЗ-12 — Добавлены выводы к вентиляторам: ЭВ2 (ВР1, ванная комната) и ЭВ5 (ВР3, санузел) — группа 4, высота 2550 мм, IP44, включение с основным светом, таймер выбега в вентиляторе.

ИЗ-13 — Общей комнатой назначен «Зал» (18,16 м²): он больше «Гостиной», проходит норму общей комнаты не менее 16 м² (СП 54.13330.2022, п. 5.11) и по концепции интерьера несёт обеденную…

ИЗ-14 — Сохраняется существующее положение: вход в санузел — из «Детской 2», перепланировка с тамбуром не выполняется.

ИЗ-15 — Доля акцента 18 % принята: ТВ-стена А красится в L481 целиком, это замысел автора, на предметы акцент не переносится.

и ещё 4 — на листе реестра

Что ждёт вашего ответа

К-1 — Окно детской 2 (поз. 9) на наружной стене В: привязки 1580…3080 в источниках нет — в экспликации скана окна этой комнаты не показано.

К-3 — Несущие стены не определены (нет плана БТИ и техзаключения): до их получения демонтаж не планируется.

К-4 — Гостиная (поз. 11): мебели в модели нет, расстановка ждёт решения заказчика.

К-5 — Гардеробная 1 (поз. 12) в натуре трапеция 2320/2132/1400, в модели прямоугольник той же площади: нужен контрольный обмер углов.

К-6 — Розетка Р7 (стиральная машина, ванная комната) стоит в 72 мм от угла при норме от 150 мм.

К-7 — Акцент L481 занимает больше порога 15 % площади поверхностей на акцентной стене А Гостиной — 16 % (проверка по доле акцента, замечание открыто намеренно).

К-8 — Графы «Пров.» и «Н. контр.» в штампе пусты: их заполняет человек, подписи проверяющего и нормоконтролёра автор проекта не ставит.

К-10 — Прямые углы помещений с кухней, санузлами, гардеробными и встроенной мебелью по скану не подтверждены (скос стен приведён к ступеням): ванная комната, тёмная комната, детская…

К-12 — Состав подрядчиков и поставщиков (кто покупает и кто монтирует радиаторы, подоконники, двери, розетки) от заказчика не получен.

К-13 — Детская 2: рабочий стол М_35 у стены Б получает боковой свет от окна справа от сидящего.

К-14 — Из чего стены под навесными шкафами — Ванная комната (стена Б, М_07), Кухня (стена А, М_23, М_24, М_25), Гардеробная 2 (стена В, М_32)? Проекта дома нет, на скане материал и…

К-15 — Стояки Ст К1-2 и Ст В1-2 (в данных (9400.

К-17 — Ведущий цвет — Paper F497 на стенах и потолке — занимает больше 80 % площади поверхностей в Тёмной комнате (87 %), Гардеробной 2 (89 %), Гардеробной 1 (86 %) и Балконе 1 (85…

К-18 — Вытяжка М_24 встроена в навесной модуль на отметке 1550 мм: её низ над электрической варочной панелью 610 мм, а фартук 650 мм при практике 450–600 мм.

и ещё 14 — на листе реестра

Предложено, ждёт подписи

ИЗ-5 — Новая группа 19 «розетки гостиной»: автомат С16, УЗО 30 мА типа А, кабель ВВГнг(А)-LS 3×2,5, 1,0 кВт, длина линии 30 м (оценка, не замер).

ИЗ-7 — Конвейер заменял акцентную стену предметами и ради порога снял её.

ИЗ-8 — Ступени контура 14840, 7770, 6600, 8030 мм (+60 мм): приведены к крайним граням помещений модели (Детская 1, Санузел).

ИЗ-9 — Добавлены: слаботочный щит ЩС (Прихожая-коридор, стена А, смещение 1380, высота 1600 мм), точки доступа АР1 (5500.

ИЗ-10 — Назначение «вытяжка М_24 (в модуле, съёмная панель)» и признак доступа access: true (не считает розетку закрытой мебелью).

					Проект: Четырёхкомнатная квартира			
	Лист	№ док.	Подпись	Дата	Ваш проект на одной странице	Стадия	Лист	Листов
Дизайнер	Кырлан А.С.			04.11.26		П	2	120

Список листов

Лист	Наименование
1	Титульный лист
2	Ваш проект на одной странице
3	Список листов
4	Список листов
5	Как читать альбом
6	План планировки от заказчика
7	План монтажный
8	Кухня (пом. 6). Монтажная схема
9	Кухня (пом. 6). Монтажная схема
10	Шкафы. Монтажная схема. Лист 1 из 3
11	Шкафы. Монтажная схема. Лист 2 из 3
12	Шкафы. Монтажная схема. Лист 3 из 3
13	Карта покрытий стен
14	Колерная карта
15	Колерная карта
16	План размещения мебели и оборудования
17	Спецификация мебели и оборудования
18	Спецификация мебели и оборудования (продолжение)
19	Спецификация мебели и оборудования (продолжение)
20	Спецификация мебели и оборудования (продолжение)
21	Ведомости изделий, техники и фурнитуры
22	План выводов сантехники
23	Схема разводки водопровода и канализации
24	Аксонометрическая схема В1 (холодное водоснабжение)
25	Аксонометрическая схема Т3 (горячее водоснабжение)
26	Аксонометрическая схема К1 (канализация)
27	Развёртки мокрых зон: выводы ВК. Ванная комната (лист 1 из 2)
28	Развёртки мокрых зон: выводы ВК. Ванная комната (лист 2 из 2)
29	Развёртки мокрых зон: выводы ВК. Кухня
30	Развёртки мокрых зон: выводы ВК. Санузел
31	Спецификация сантехнического оборудования
32	Раскладка плитки. Ванная комната. Развёртки стен
33	Раскладка плитки. Санузел. Развёртки стен
34	План размещения дверей
35	Ведомость заполнения проёмов
36	План потолков
37	Разрезы и узлы потолков
38	Разрезы и узлы потолков (продолжение)
39	Сечения потолков М 1:10
40	Сечения потолков М 1:10
41	Однолинейная схема щита
42	Однолинейная схема щита (продолжение)
43	План розеток и электровыводов
44	План слаботочных сетей
45	План освещения
46	Техническое задание на подбор светильников
47	Управление светильниками
48	План вентиляции
49	План отопления
50	План покрытий пола
51	Раскладка плитки. Планы полов
52	Раскладка плитки. Фартук кухни
53	Развёртка стены А. Зал (пом. 1)
54	Привязки электроточек, стена А. Зал (пом. 1)
55	Развёртка стены Б. Зал (пом. 1)
56	Развёртка стены В. Зал (пом. 1)
57	Развёртка стены Г. Зал (пом. 1)
58	Развёртки стен А, Б. Ванная комната (пом. 2)
59	Развёртки стен В, Г. Ванная комната (пом. 2)
60	Привязки электроточек и выводов ВК, стены Б, В. Ванная комната (пом. 2)

					Проект: Четырёхкомнатная квартира
	Лист	№ док.	Подпись	Дата	
Дизайнер	Кырлан А.С.			04.11.26	Список листов
					Стадия: П; Лист: 3; Листов: 120

Список листов (продолжение)

Лист	Наименование
61	Развёртки стен А, Б, В. Тёмная комната (пом. 3)
62	Развёртка стены Г. Тёмная комната (пом. 3)
63	Развёртка стены А. Детская 1 (пом. 4)
64	Развёртка стены Б. Детская 1 (пом. 4)
65	Развёртка стены В. Детская 1 (пом. 4)
66	Развёртка стены Г. Детская 1 (пом. 4)
67	Развёртки стен А, Б. Коридор (пом. 5)
68	Развёртка стены В. Коридор (пом. 5)
69	Развёртка стены А. Кухня (пом. 6), кухонный фронт
70	Привязки электроточек, стена А. Кухня (пом. 6)
71	Развёртка стены Б. Кухня (пом. 6)
72	Развёртка стены В. Кухня (пом. 6)
73	Развёртка стены Г. Кухня (пом. 6)
74	Развёртки стен А, Б. Прихожая-коридор (пом. 7)
75	Развёртки стен В, Г. Прихожая-коридор (пом. 7)
76	Развёртки стен А, Б, В. Гардеробная 2 (пом. 8)
77	Развёртка стены Г. Гардеробная 2 (пом. 8)
78	Развёртка стены А. Детская 2 (пом. 9)
79	Развёртка стены Б. Детская 2 (пом. 9)
80	Привязки электроточек, стена Б. Детская 2 (пом. 9)
81	Развёртка стены В. Детская 2 (пом. 9)
82	Развёртка стены Г. Детская 2 (пом. 9)
83	Развёртки стен А, Б, В. Санузел (пом. 10)
84	Привязки электроточек и выводов ВК, стена Б. Санузел (пом. 10)
85	Развёртка стены Г. Санузел (пом. 10)
86	Развёртка стены А. Гостиная (пом. 11)
87	Развёртка стены Б. Гостиная (пом. 11)
88	Развёртки стен В, Г. Гостиная (пом. 11)
89	Развёртки стен. Гардеробная 1 (пом. 12)
90	Развёртки стен А, Б. Балкон 1 (пом. 13)
91	Развёртки стен В, Г. Балкон 1 (пом. 13)
92	Открытые вопросы, принятые допущения и конфликты. Лист 1 из 5
93	Открытые вопросы, принятые допущения и конфликты. Лист 2 из 5
94	Открытые вопросы, принятые допущения и конфликты. Лист 3 из 5
95	Открытые вопросы, принятые допущения и конфликты. Лист 4 из 5
96	Открытые вопросы, принятые допущения и конфликты. Лист 5 из 5
Д_1	Система хранения М_07
Д_2	Система хранения М_08
Д_3	Система хранения М_09
Д_4	Шкаф распашной М_15
Д_5	Система хранения М_17
Д_6	Система хранения М_18
Д_7	Шкаф-купе М_28
Д_8	Система хранения М_31
Д_9	Система хранения М_32
Д_10	Шкаф распашной М_34
Д_11	Система хранения М_38
Д_12	Система хранения М_39
Д_13	Система хранения М_40
Д_14	Кухня (пом. 6). Развёртка гарнитура
Д_15	Кухня (пом. 6). Развёртка гарнитура
Д_16	Остров М_26 (пом. 6). Чертёж изделия
С1	Ведомость отделки помещений. Лист 1 из 3
С2	Ведомость отделки помещений. Лист 2 из 3
С3	Ведомость отделки помещений. Лист 3 из 3
С4	Спецификация отделочных материалов
С5	Спецификация отделочных материалов
С6	Список покупок
С7	Список покупок (окончание)
С8	Узлы

Общие указания

1. Размеры даны в мм от чистовых поверхностей стен: слой штукатурки 20 мм по блоку и 5 мм шпаклёвки по ГКЛ учтён. Перед заказом встроенной мебели — контрольный обмер после штукатурки.
2. Привязки мебели — от стен и углов помещения, а не от другой мебели.
3. Розетки, выводы и выключатели под мебель — см. лист 43 «План розеток и электровыводов»; сантехприборы и выводы воды — лист 22.
4. План расстановки не является документацией для изготовления мебели: изделия — по чертежам мебельщика; покупную мебель заменять только на изделия не больше габарита из спецификации (лист 17).
5. Встроенная мебель «стена в стену» — с зазором 10 мм с каждой стороны или с компенсаторами.
6. Развёртки — вид на стену изнутри помещения, по часовой стрелке; расположение стен на схеме листа развёртки; размеры — в мм по чистовым поверхностям; отметки — в м от ±0,000; высоты Н — от чистого пола помещения до оси изделия, у декора — до центра.
7. Красная цепочка — привязки электроточек и выводов по осям от угла чистовых стен; высота Н — у знака, от чистого пола до оси; высоты мебели, проёмов и границ отделки колонкой отметок слева. Стена с 5 и более точками или с мелкими звеньями привязок показана двумя видами: архитектурная развёртка (мебель, отделка, проёмы, высоты) и вид «Привязки» на отдельном листе — точки и выводы с марками, одна цепочка по осям и таблица привязок (каждая точка — строка).
8. У знака электроточки: марка (Р — розетка, S — выключатель, Св — светильник, ЭВ вывод кабеля), ×N — число постов в рамке, гр. — группа щита, Н — высота оси от чистого пола, мм; группы по клавишам выключателя — на листе выключателей.
9. Схема мебели, приборов и декора не является технической документацией для производства мебели; габариты — по паспортам изделий.
10. Марки позиций: М_NN — мебель, ОБ_NN — оборудование, С_NN — сантехника; О-N отделка (ведомость отделочных материалов, серия С).
11. Размеры мебели и изделий на заказ уточнить по месту после отделочных работ.

					Проект: Четырёхкомнатная квартира
	Лист	№ док.	Подпись	Дата	
Дизайнер	Кырлан А.С.			04.11.26	Список листов
					Стадия: П; Лист: 4; Листов: 120

выпуск 04.11.2026 № 2391fcbada · стр. 4 из 120

Что в альбоме

Альбом — дизайн-проект с рабочими чертежами для ремонта. Листы идут в порядке работ: титул и вводные, реестр открытых вопросов и решений, планы (обмер, монтаж стен, мебель, двери, потолки, полы), инженерия (сантехника, электрика, вентиляция и отопление), развёртки стен с визуализациями помещений, чертежи мебели, ведомости материалов и узлы.

Вам как заказчику — титул, эта вводная, «Ваш проект на одной странице», реестр вопросов, план мебели, визуализации и развёртки, ведомости мебели и материалов. Подрядчику — всё остальное: монтажные планы, привязки выводов и розеток, узлы, ведомости объёмов.

Знаки на листах

Без знака — решение утверждено или подтверждено обмером.

Что проверить до ремонта

1. Розетки у кровати и рабочего места: хватает ли их с каждой стороны кровати и над столом (план розеток — лист 43).

2. Выводы под технику — варочная панель, духовка, посудомойка, стиральная машина, бойлер: совпадают ли с выбранными моделями (листы 17, 18, 19, 20, 43).

3. Высоты розеток, выключателей и выводов даны от чистого пола: если мебель или техника будут другими — скажите до штробления стен.

Номера записей

К-N — открытый вопрос: чего не хватает или что выбрать (варианты и рекомендация — в тексте). Пока ответа нет, действует строка «если решения нет».

Кф-N — конфликт между разделами (например, мебель и радиатор в одном месте); закрывается решением, которое записывается как ИЗ-N.

ИЗ-N — изменение проекта: что было, что стало и кто утвердил. Изменение без подписи предложение.

Все записи — на листе реестра сразу после вводных; на других листах на них стоят ссылки.

Почему альбом предварительный

Обмера на объекте не было: размеры взяты с плана заказчика. Технические условия (мощность, вода, вентиляция дома) не получены, часть решений ждёт вашего ответа. Пока в реестре есть открытые вопросы, альбом предварительный — пометка в штампе снимается закрытием вопросов, а не стиранием.

Правку к любому листу можно оставить по кнопке «Правка к листу» или на сайте студии: дизайн-студия-квартир.рф — укажите номер листа и что изменить.

3 круга правок входят в цену; условия — в договоре и на странице вашего заказа на сайте студии.


Шифр проекта ГД-2026-004-АИ

					Проект: Четырёхкомнатная квартира
	Лист	№ док.	Подпись	Дата	
Дизайнер	Кырлан А.С.			04.11.26	Как читать альбом

Стадия	Лист	Листов
П	5	120

Отметки по высоте

±0,000	чистый пол пом. 1, 3–9, 11, 12; отсчёт высот
−0,015	чистый пол пом. 2, 10, ниже на 15 мм
−0,030	чистый пол пом. 13, ниже на 30 мм
−0,170	верх плиты — расчёт, не замер (задание на обмер)
сущ. пол	снимается до плиты; не замерен (задание на обмер)

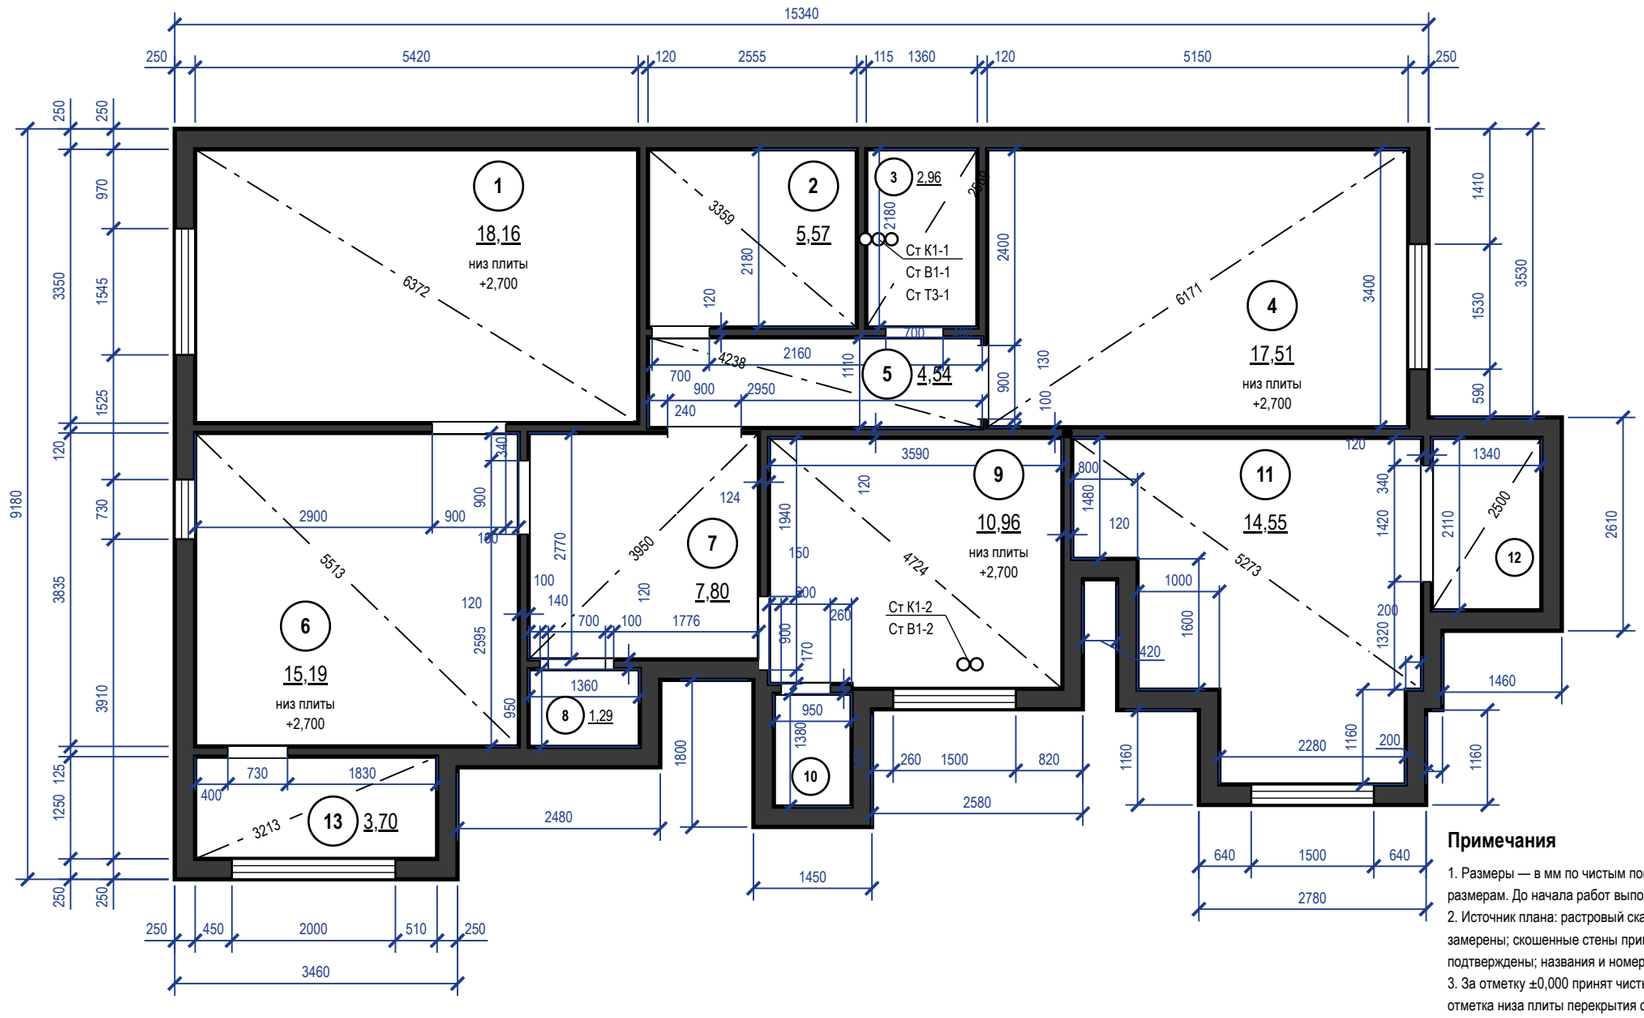

Экспликация помещений

№	Наименование	Площадь, м²
1	Зал	18,16
2	Ванная комната	5,57
3	Тёмная комната	2,96
4	Детская 1	17,51
5	Коридор	4,54
6	Кухня	15,19
7	Прихожая-коридор	7,80
8	Гардеробная 2	1,29
9	Детская 2	10,96
10	Санузел	1,31
11	Гостиная	14,55
12	Гардеробная 1	2,83
13	Балкон 1 *	3,70
	Итого (общая площадь)	**102,67**


Условные обозначения

- существующие стены (сечение)
- окно (рама, остекление)
- проём существующий, без заполнения (откосы)
- стояк: К1 — канализация, В1 — ХВС, Т3 — ГВС
- диагональ помещения — контроль прямоугольности
- (1) номер помещения, площадь м²

Примечания

1. Размеры — в мм по чистым поверхностям стен до отделки (по плану заказчика); площади — в м² по тем же размерам. До начала работ выполнить контрольный обмер.
2. Источник плана: растровый скан плана заказчика, размеры сняты с размерных цепочек, на объекте не замерены; скошенные стены приведены к ступеням (на плане не натура), углы 90° и диагонали не подтверждены; названия и номера помещений со сканом не сверены.
3. За отметку ±0,000 принят чистый пол, не существующий (блок отметок). «Низ плиты» у марки помещения отметка низа плиты перекрытия от ±0,000, как на развёртках и плане потолков (не высота потолка: потолок по плану потолков).
4. Толщины стен: наружные 250 мм, перегородки 120 мм; отличающиеся толщины и уступы — размерами на плане.
5. Несущие стены не определены: до технического заключения все стены считать несущими; проёмы и штробы в них не выполнять.
6. Дверные проёмы показаны без заполнения (двери — лист 35); высота дверных проёмов 2100 мм; низ окон (подоконник) 800, 900 мм от чистого пола, высота окон 1600, 1700 мм.
7. Диагонали — контрольные размеры; расхождение более 5 мм подписать на плане как перекос.
8. Размеры проверить на месте до начала работ; расхождение контрольных промеров ≤ 2 %.
9. Помещения, отмеченные *, в общую площадь квартиры и в итоги не входят.
10. Размеры короче 1 мм на листе цепочкой не показаны (две выносные линии на таком расстоянии сливаются): пом. 5, стена А — 50 мм от угла до проёма.

					Проект: Четырёхкомнатная квартира — **М 1:75**
	Лист	№ док.	Подпись	Дата	План планировки от заказчика
Дизайнер	Кырлан А.С.			04.11.26	Стадия: П · Лист: 6 · Листов: 120

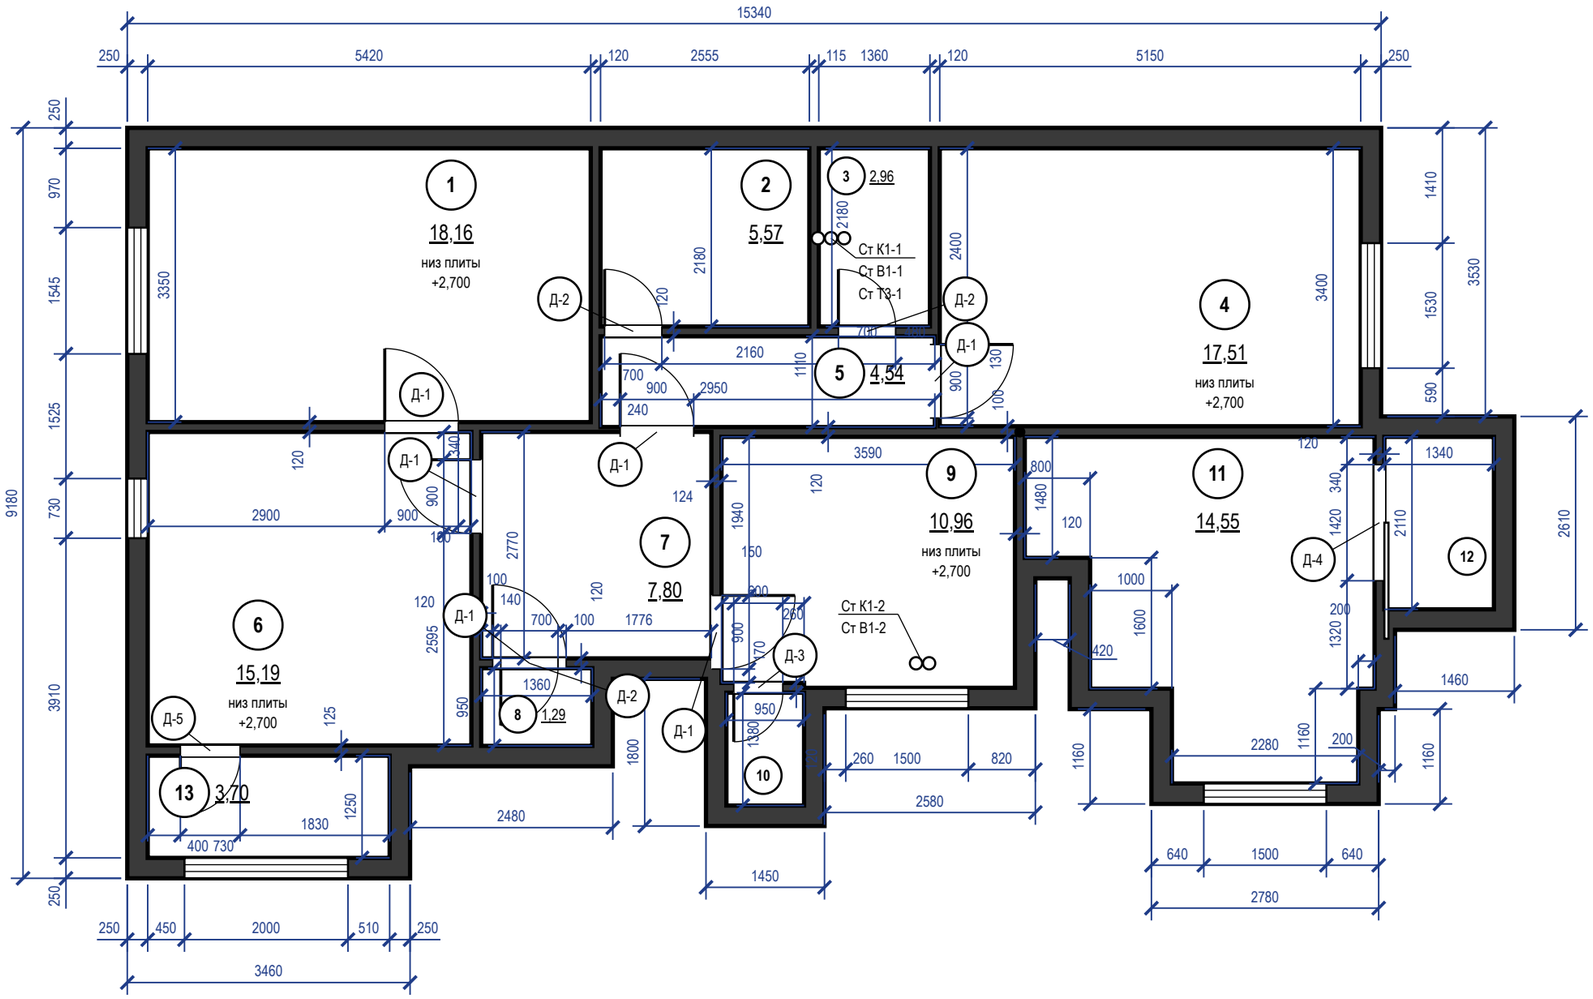

Экспликация помещений

№	Наименование	Площадь, м²
1	Зал	18,16
2	Ванная комната	5,57
3	Тёмная комната	2,96
4	Детская 1	17,51
5	Коридор	4,54
6	Кухня	15,19
7	Прихожая-коридор	7,80
8	Гардеробная 2	1,29
9	Детская 2	10,96
10	Санузел	1,31
11	Гостиная	14,55
12	Гардеробная 1	2,83
13	Балкон 1 *	3,70
	Итого (общая площадь)	**102,67**

Таблица проёмов


Марка	Наименование	Проём ш×в, мм	Полотно (расч.)
Д-1	Дверь распашная	900×2100	800×2000
Д-2	Дверь распашная	700×2100	600×2000
Д-3	Дверь распашная	600×2100	не задано (записи реестра нет)
Д-4	Дверь раздвижная	1420×2100	не задано (записи реестра нет)
Д-5	Дверь распашная	730×2100	не задано (записи реестра нет)

Примечания


1. Размеры — в мм от чистовых поверхностей стен до отделки; размеры уточнить по месту до начала работ.
2. Д-N, ПР-N в кружке — марка проёма: проём и полотно — по таблице проёмов, «расч.» полотно по проёму, заказ — по выбранной модели; ведомость, отделка и фурнитура — лист 35.
3. Несущие стены не изменять: проёмы, ниши и штробы в них — только по техническому заключению.
4. «расч.» — полотно, выведенное из проёма по запасу каталогов; заказ — по таблице проёмов выбранной модели; Д-1, Д-2: проём 2100, а под полотно 2000 по каталогам нужен 2040–2080, под 2100 — 2140–2180: высоту проёма — по модели; Д-3: проём 600×2100 вне ряда стандартных полотен — полотно задать при выборе модели; Д-4: раздвижная, полотно — по системе — полотно задать при выборе модели; Д-5: проём 730×2100 вне ряда стандартных полотен — полотно задать при выборе модели.
5. Размеры короче 1 мм на листе цепочкой не показаны (две выносные линии на таком расстоянии сливаются): пом. 5, стена А — 50 мм от угла до проёма.

					Проект: Четырёхкомнатная квартира — **М 1:75**
	Лист	№ док.	Подпись	Дата	План монтажный
Дизайнер	Кырлан А.С.			04.11.26	Стадия: П · Лист: 7 · Листов: 120

Привязка выводов и крепление модулей

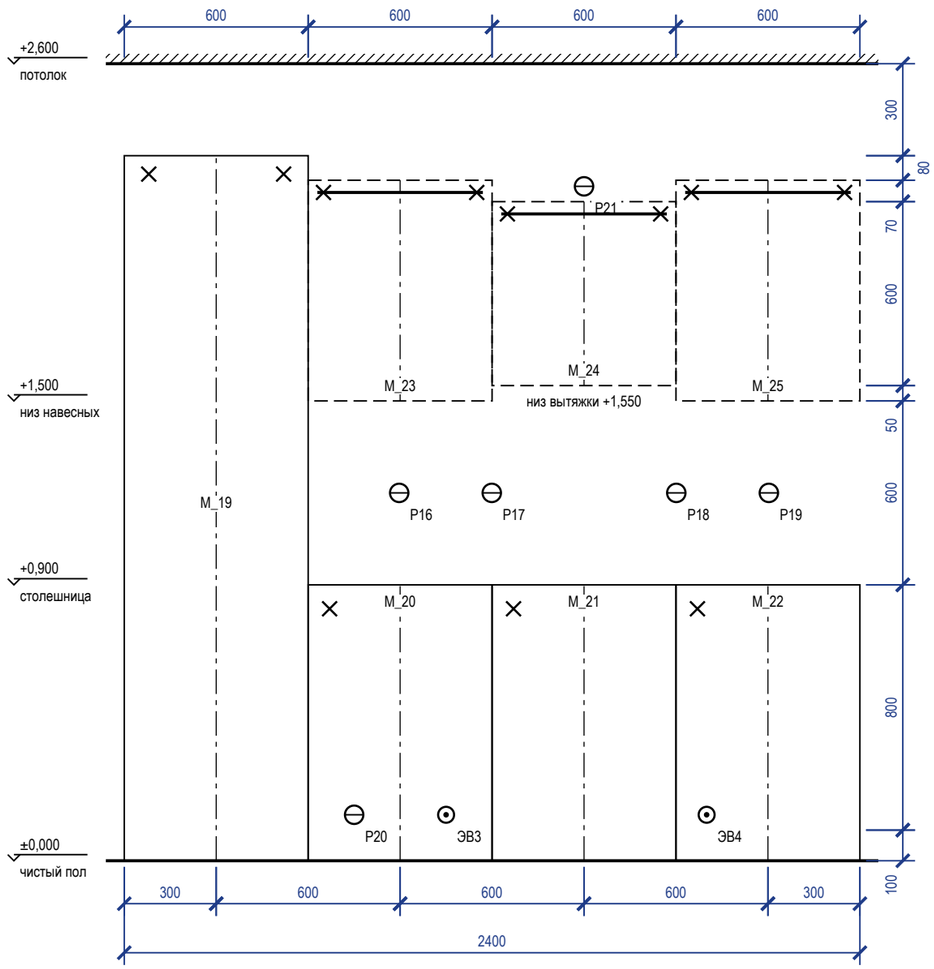

План столешницы

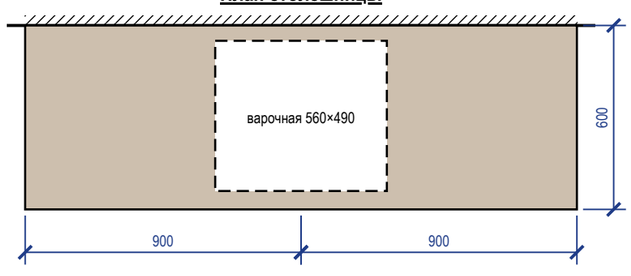

Привязка выводов к осям модулей

Код	Назначение	Модуль	От оси, мм	H, мм	Размещение
P20	розетка — холодильник встроенный M_19 (розетка в модуле M_20)	M_20	−150	150	в соседнем модуле, за ящиком
P16	розетка ×2 — фартук: мелкая техника	M_20	−3	1200	над столешницей (фартук)
ЭВ3	вывод кабеля — варочная панель M_21	M_20	+150	150	в соседнем модуле, за ящиком
P17	розетка ×2 — фартук: мелкая техника	M_20	+299	1200	над столешницей (фартук)
P21	розетка — вытяжка M_24 (в модуле, съёмная панель)	M_24	0	2200	в навесном модуле
P18	розетка ×2 — фартук: мелкая техника	M_21	+301	1200	над столешницей (фартук)
ЭВ4	вывод кабеля — духовой шкаф M_21 (вывод в соседнем модуле M_22)	M_22	−200	150	в соседнем модуле, за ящиком
P19	розетка ×2 — фартук: мелкая техника	M_22	+3	1200	над столешницей (фартук)

Зазоры под отделку

Поверхность	Отделка	Зазор, мм	Учесть
фартук	керамогранит	10	от чернового основания до корпуса навесных и столешницы
стены	окраска	5	под штукатурку и шпаклёвку за пеналом
пол	инженерная доска		цоколь — после укладки пола, опоры ±20 мм

Условные обозначения


- нижний модуль, пенал (контур)
- невидимый контур: навесной модуль, корпус под столешницей
- ось модуля (от неё — привязка вывода)
- анкер / уголок крепления к стене
- розетка на стене
- вывод кабеля к технике
- B1 — вывод воды B1 / Т3, канализации К1

Примечания

1. Выводы — по проекту электрики и ВК; привязка по горизонтали — от оси модуля (плюс — вправо по виду), по высоте — от чистого пола до оси вывода.
2. Пенал — уголки к стене 2 шт. сверху; нижние модули — стяжками между собой и уголком к стене; ряд выставить по уровню опорами цоколя.
3. Розетки над столешницей — не ниже 150 мм над ней и не за корпусом техники; розетка за ПММ, духовым шкафом и холодильником — только в соседнем модуле или в зоне цоколя с доступом.
4. Столешница — вырезы по шаблонам выбранных моделей мойки и варочной панели; торцы у стены — герметик, пристеночный плинтус.

					Проект: Четырёхкомнатная квартира	**М 1:20**
	Лист	№ док.	Подпись	Дата		
Дизайнер	Кырлан А.С.			04.11.26	Кухня (пом. 6). Монтажная схема	Стадия: П; Лист: 8; Листов: 120

Привязка выводов и крепление модулей

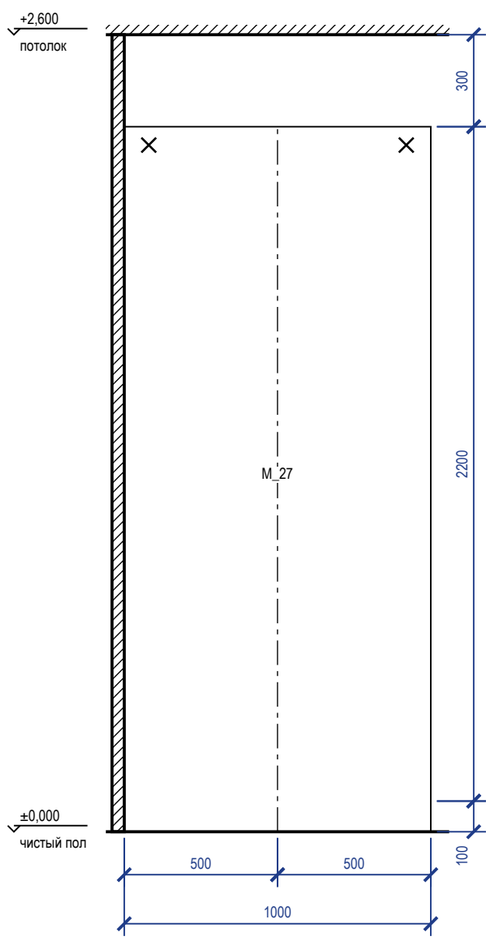

Привязка выводов к осям модулей

Код	Назначение	Модуль	От оси, мм	Н, мм	Размещение

Зазоры под отделку

Поверхность	Отделка	Зазор, мм	Учесть
фартук	керамогранит	10	от чернового основания до корпуса навесных и столешницы
стены	окраска	5	под штукатурку и шпаклёвку за пеналом
пол	инженерная доска		цоколь — после укладки пола, опоры ±20 мм

Условные обозначения


- нижний модуль, пенал (контур)
- ось модуля (от неё — привязка вывода)
- анкер / уголок крепления к стене
- розетка на стене
- вывод кабеля к технике
- B1 — вывод воды B1 / Т3, канализации К1

Примечания


1. Выводы — по проекту электрики и ВК; привязка по горизонтали — от оси модуля (плюс — вправо по виду), по высоте — от чистого пола до оси вывода.
2. Пенал — уголки к стене 2 шт. сверху; нижние модули — стяжками между собой и уголком к стене; ряд выставить по уровню опорами цоколя.
3. Розетки над столешницей — не ниже 150 мм над ней и не за корпусом техники; розетка за ПММ, духовым шкафом и холодильником — только в соседнем модуле или в зоне цоколя с доступом.
4. Столешница — вырезы по шаблонам выбранных моделей мойки и варочной панели; торцы у стены — герметик, пристеночный плинтус.

					Проект: Четырёхкомнатная квартира — **М 1:20**
	Лист	№ док.	Подпись	Дата	
Дизайнер	Кырлан А.С.			04.11.26	Кухня (пом. 6). Монтажная схема
					Стадия: П; Лист: 9; Листов: 120


M_07 (пом. 2)

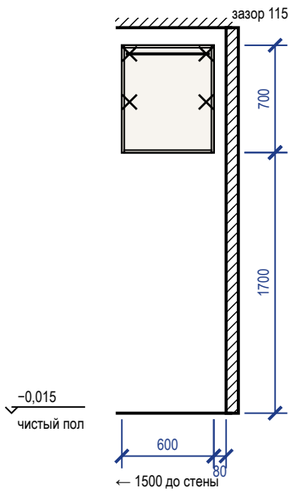


Система хранения M_08 (пом. 3)

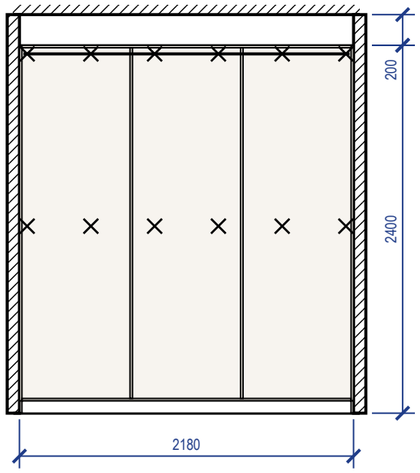


Система хранения M_09 (пом. 3)

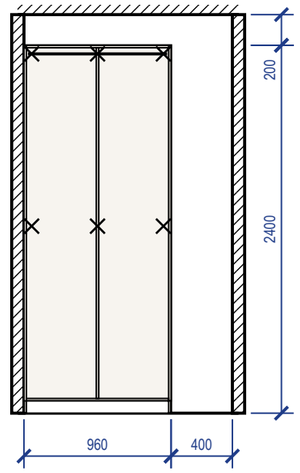

Шкаф распашной M_15 (пом. 4)

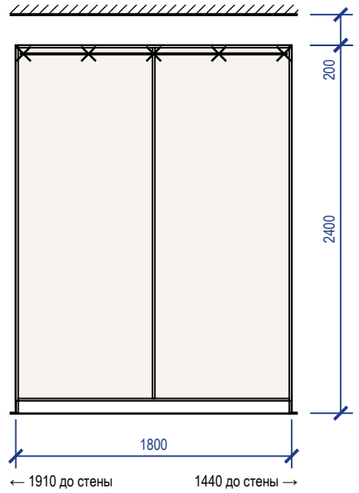

Система хранения M_17 (пом. 4)

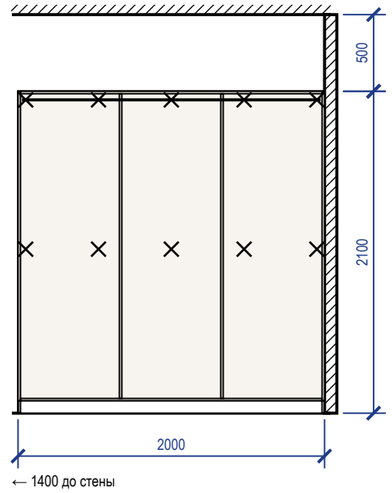

Крепление и зазоры под отделку (изделия листа 1)

Марка	Помещение, стена	Основание	Отделка стены	Зазор, мм	Крепёж по планке	От опрокидывания
M_07	Ванная комната (2), стена Б	по основанию — см. таблицу крепежа	плитка	10	анкер 4 шт. (2 ряда)	крепление к стене, 2 точки
M_08	Тёмная комната (3), стена Б	по основанию — см. таблицу крепежа	окраска	5	анкер 12 шт. (2 ряда)	крепление к стене, 4 точки
M_09	Тёмная комната (3), стена А	по основанию — см. таблицу крепежа	окраска	5	анкер 6 шт. (2 ряда)	крепление к стене, 3 точки
M_15	Детская 1 (4), стена В	по основанию — см. таблицу крепежа	окраска	5	анкер 5 шт., шаг 425	уголок к стене, 3 шт.
M_17	Детская 1 (4), стена Г	по основанию — см. таблицу крепежа	окраска	5	анкер 10 шт. (2 ряда)	крепление к стене, 3 точки

Крепёж по основанию стены

Основание стены	Крепёж
бетон, ж/б	анкер-шуруп 7,5×72 или дюбель 8×60 с шурупом 5×70
кирпич полнотелый	дюбель 8×80 с шурупом 5×90
газобетон, пазогребень	дюбель для газобетона 10×100 или химический анкер
гипсокартон	закладная до обшивки (брус 40×80 или фанера 18 мм), саморез в закладную

Условные обозначения


- анкер / уголок крепления к стене
- корпус и полки ЛДСП (вид на стену)
- компенсатор — короб до потолка

Примечания


1. Установочные размеры — от чистого пола и чистых стен; перед установкой контрольный замер после отделки.
2. Порядок: корпус выставить по уровню опорами цоколя → закрепить к стене по задней планке → навесить двери и фасады, отрегулировать зазоры → подогнать и закрепить компенсатор.
3. Анкеры — с шагом не более 500 мм, не ближе 50 мм от края планки; на ГКЛ только в закладную, установленную до обшивки.
4. Скрытые коммуникации под анкеры проверить детектором; трассы электрики по плану розеток.
5. Монтажная схема на 3 листах, лист 1 из 3; продолжение — на следующем листе схемы. Условные обозначения, таблица крепежа по основанию и примечания повторены на каждом листе.

					Проект: Четырёхкомнатная квартира	**М 1:40**
	Лист	№ док.	Подпись	Дата		
Дизайнер	Кырлан А.С.			04.11.26	Шкафы. Монтажная схема. Лист 1 из 3	Стадия: П; Лист: 10; Листов: 120


Система хранения М_18 (пом. 5)

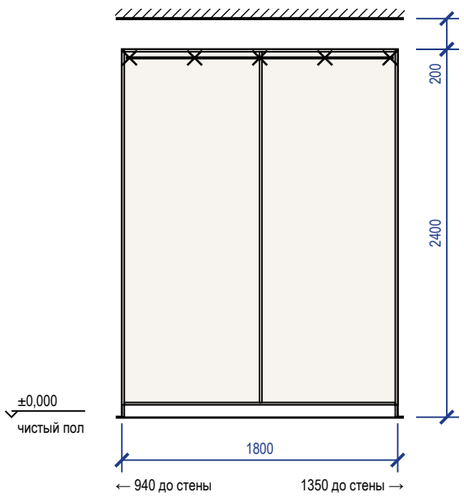


Шкаф-купе М_28 (пом. 7)

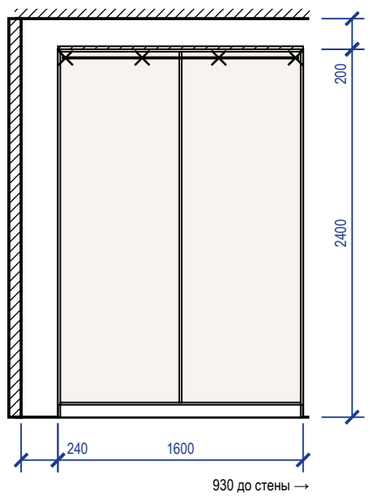


Система хранения М_31 пом. 8

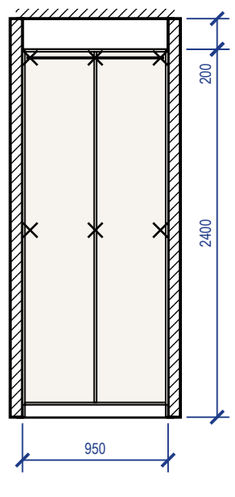

Система хранения М_32 (пом. 8)

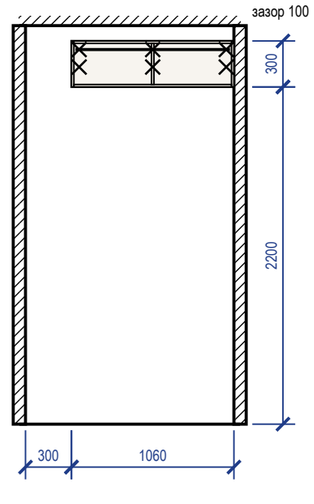

Шкаф распашной М_34 (пом. 9)

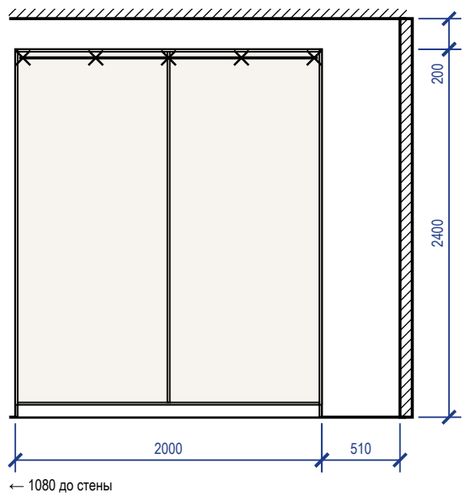

Крепление и зазоры под отделку (изделия листа 2)

Марка	Помещение, стена	Основание	Отделка стены	Зазор, мм	Крепёж по планке	От опрокидывания
М_18	Коридор (5), стена А	по основанию — см. таблицу крепежа	окраска	5	анкер 5 шт., шаг 425	крепление к стене, 4 точки
М_28	Прихожая-коридор (7), стена Б	по основанию — см. таблицу крепежа	окраска	5	анкер 4 шт., шаг 500	крепление к стене, 3 точки
М_31	Гардеробная 2 (8), стена Б	по основанию — см. таблицу крепежа	окраска	5	анкер 6 шт. (2 ряда)	крепление к стене, 3 точки
М_32	Гардеробная 2 (8), стена В	по основанию — см. таблицу крепежа	окраска	5	анкер 6 шт. (2 ряда)	крепление к стене, 4 точки
М_34	Детская 2 (9), стена А	по основанию — см. таблицу крепежа	окраска	5	анкер 5 шт., шаг 475	уголок к стене, 3 шт.

Крепёж по основанию стены

Основание стены	Крепёж
бетон, ж/б	анкер-шуруп 7,5×72 или дюбель 8×60 с шурупом 5×70
кирпич полнотелый	дюбель 8×80 с шурупом 5×90
газобетон, пазогребень	дюбель для газобетона 10×100 или химический анкер
гипсокартон	закладная до обшивки (брус 40×80 или фанера 18 мм), саморез в закладную

Условные обозначения


- анкер / уголок крепления к стене
- корпус и полки ЛДСП (вид на стену)
- компенсатор — короб до потолка

Примечания


1. Установочные размеры — от чистого пола и чистых стен; перед установкой контрольный замер после отделки.
2. Порядок: корпус выставить по уровню опорами цоколя → закрепить к стене по задней планке → навесить двери и фасады, отрегулировать зазоры → подогнать и закрепить компенсатор.
3. Анкеры — с шагом не более 500 мм, не ближе 50 мм от края планки; на ГКЛ только в закладную, установленную до обшивки.
4. Скрытые коммуникации под анкеры проверить детектором; трассы электрики по плану розеток.
5. Монтажная схема на 3 листах, лист 2 из 3; продолжение — на следующем листе схемы. Условные обозначения, таблица крепежа по основанию и примечания повторены на каждом листе.

					Проект: Четырёхкомнатная квартира	М 1:40
	Лист	№ док.	Подпись	Дата		
Дизайнер	Кырлан А.С.			04.11.26	Шкафы. Монтажная схема. Лист 2 из 3	Стадия: П; Лист: 11; Листов: 120


Система хранения М_38 (пом. 12)

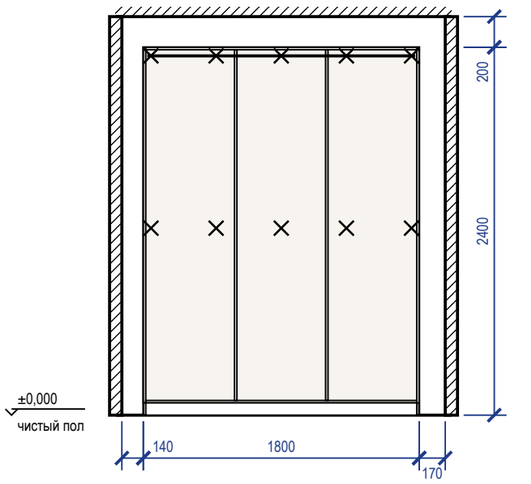

Система хранения М_39 пом. 13

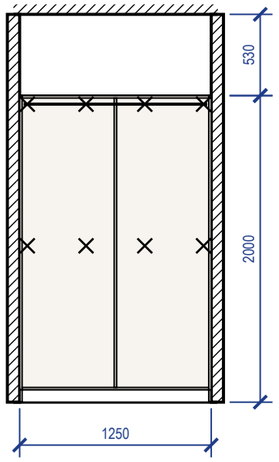

Система хранения М_40 пом. 13

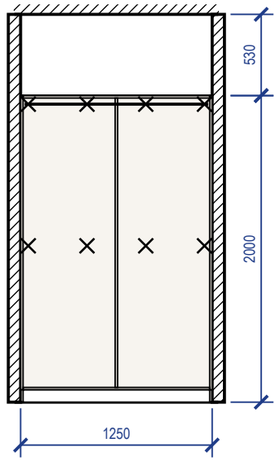

Крепление и зазоры под отделку (изделия листа 3)

Марка	Помещение, стена	Основание	Отделка стены	Зазор, мм	Крепёж по планке	От опрокидывания
М_38	Гардеробная 1 (12), стена Б	по основанию — см. таблицу крепежа	окраска	5	анкер 10 шт. (2 ряда)	крепление к стене, 4 точки
М_39	Балкон 1 (13), стена Б	по основанию — см. таблицу крепежа	окраска	5	анкер 8 шт. (2 ряда)	крепление к стене, 3 точки
М_40	Балкон 1 (13), стена Г	по основанию — см. таблицу крепежа	окраска	5	анкер 8 шт. (2 ряда)	крепление к стене, 3 точки

Крепёж по основанию стены

Основание стены	Крепёж
бетон, ж/б	анкер-шуруп 7,5×72 или дюбель 8×60 с шурупом 5×70
кирпич полнотелый	дюбель 8×80 с шурупом 5×90
газобетон, пазогребень	дюбель для газобетона 10×100 или химический анкер
гипсокартон	закладная до обшивки (брус 40×80 или фанера 18 мм), саморез в закладную


Условные обозначения

- анкер / уголок крепления к стене
- корпус и полки ЛДСП (вид на стену)
- компенсатор — короб до потолка

Примечания

1. Установочные размеры — от чистого пола и чистых стен; перед установкой контрольный замер после отделки.
2. Порядок: корпус выставить по уровню опорами цоколя → закрепить к стене по задней планке → навесить двери и фасады, отрегулировать зазоры → подогнать и закрепить компенсатор.
3. Анкеры — с шагом не более 500 мм, не ближе 50 мм от края планки; на ГКЛ только в закладную, установленную до обшивки.
4. Скрытые коммуникации под анкеры проверить детектором; трассы электрики по плану розеток.
5. Монтажная схема на 3 листах, лист 3 из 3. Условные обозначения, таблица крепежа по основанию и примечания повторены на каждом листе.

					Проект: Четырёхкомнатная квартира	**М 1:40**
	Лист	№ док.	Подпись	Дата		
Дизайнер	Кырлан А.С.			04.11.26	Шкафы. Монтажная схема. Лист 3 из 3	Стадия: П; Лист: 12; Листов: 120

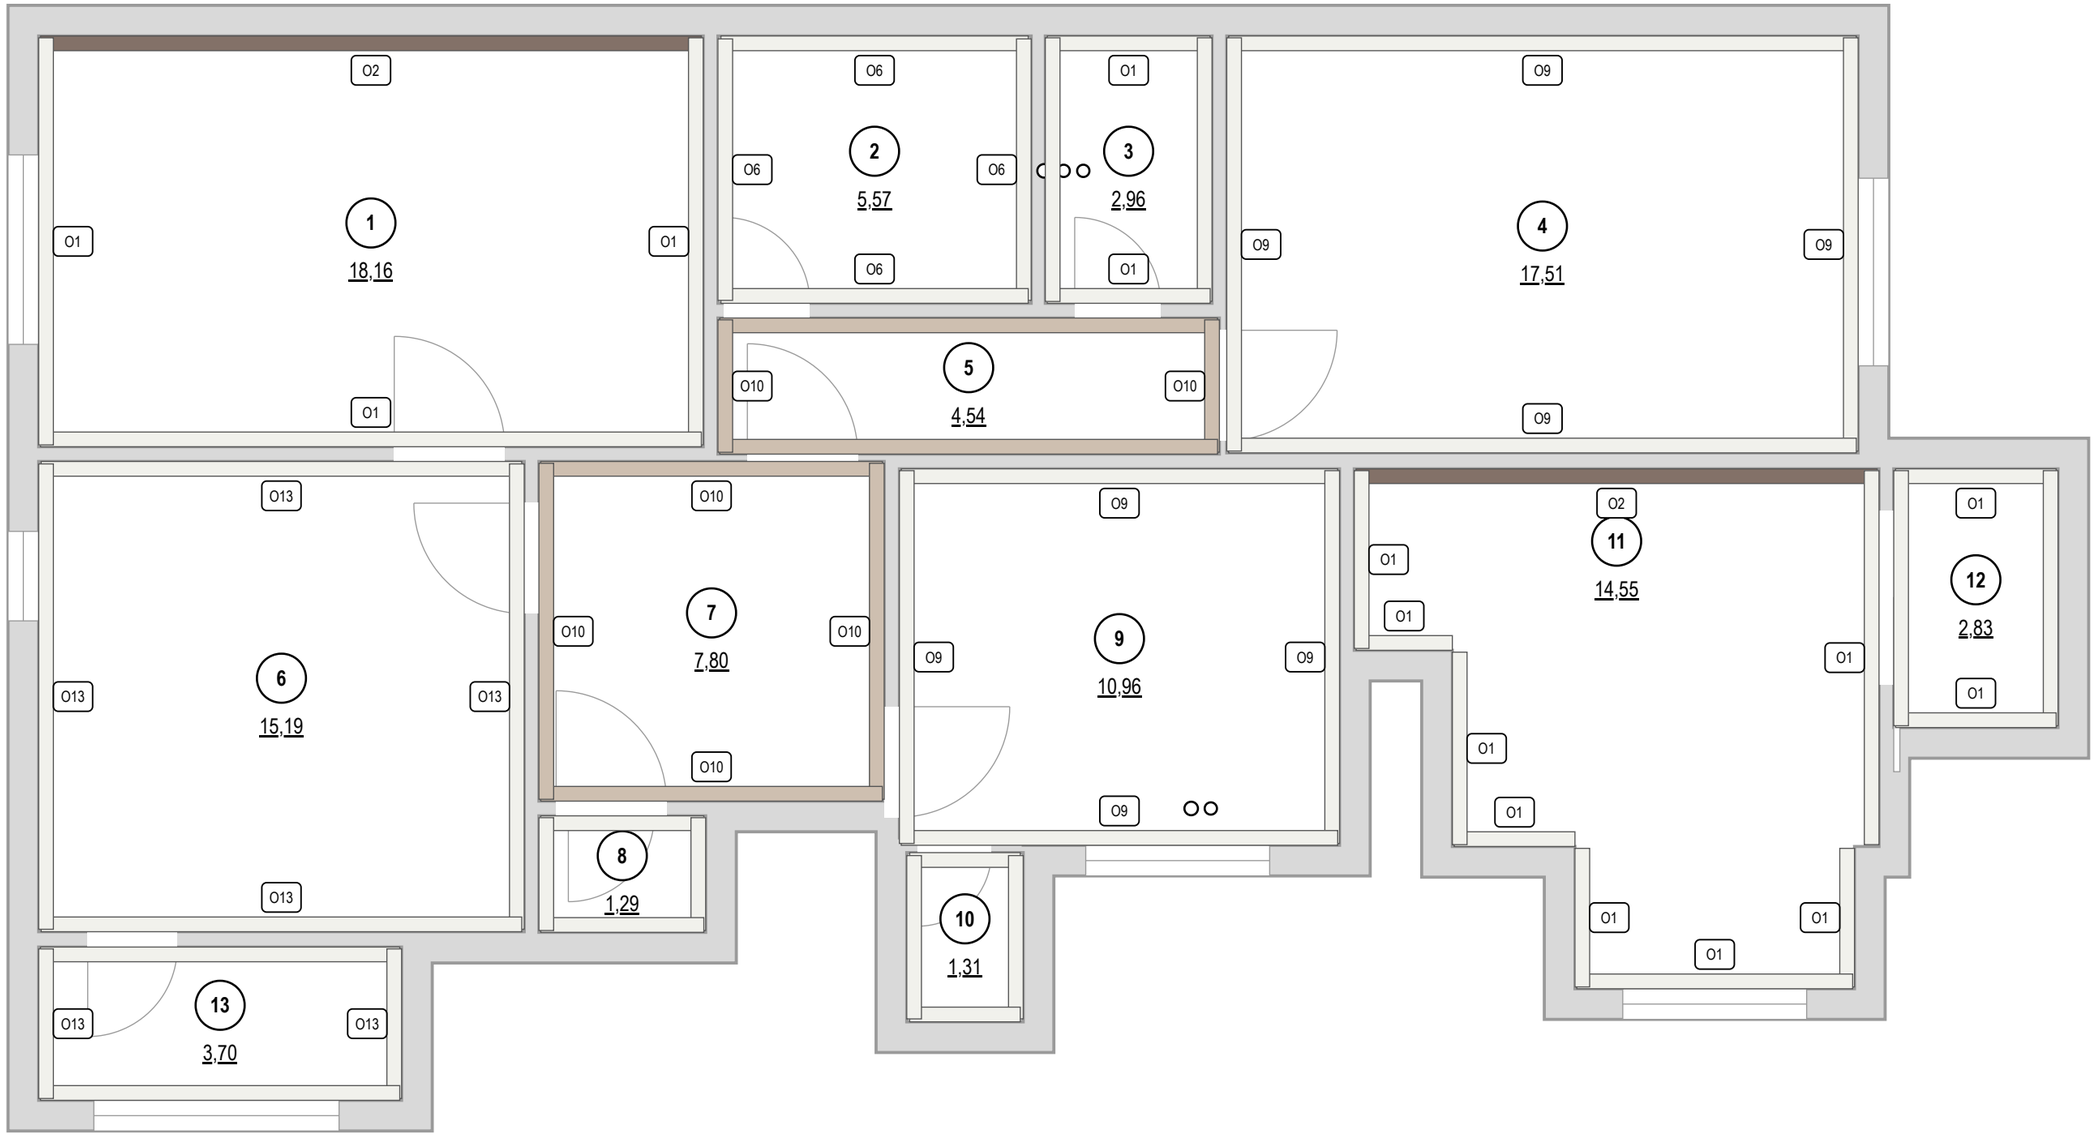

Покрытия стен

Марка	Покрытие	Помещение: S, м²	Итого, м²
O1	окраска Tikkurila · F497 «Paper»	1: 27,2; 3: 16,6; 8: 8,3; 11: 27,0; 12: 14,6	93,8
O2	окраска Tikkurila · L481 «Silhouette»	1: 13,5; 11: 11,1	24,5
O6	облицовка плиткой · «тон Paper F497» 600×600 мм	2: 21,9; 10: 10,0	31,8
O9	окраска Tikkurila · F497 «Paper»	4: 40,1; 9: 29,1	69,3
O10	окраска Tikkurila · J484 «Castle»	5: 20,0; 7: 20,0	40,0
O13	окраска Tikkurila · F497 «Paper»	6: 32,9; 13: 16,4	49,3

Площади — нетто, по развёрткам (за вычетом проёмов и фартука); высоты помещений — от чистого пола.

	Лист	№ док.	Подпись	Дата
Дизайнер	Кырлан А.С.			04.11.26

Проект: Четырёхкомнатная квартира — **М 1:50**

Карта покрытий стен

Стадия	Лист	Листов
П	13	120

Колерная карта по помещениям

Помещение	Поверхность	Образец	Поз.	Система и код цвета	Производитель, линейка / материал, артикул	Блеск	Класс истирания	LRV	Площадь
1. Зал 18,16 м²	стены		**К1**	Tikkurila F497	Tikkurila · Optiva 5 Matt	матовая	2	88	25,9 м²
	акцент А		**К2**	Tikkurila L481	Tikkurila · Optiva 5 Matt	матовая	2	18	13,6 м²
	потолок		**К3**	Tikkurila F497	Tikkurila · Anti-Reflex 2	глубокомат.	2	88	18,2 м²
	пол		**КМ1**	по образцу	инженерная доска · аналог по хар.				18,2 м²
	плинтус		**К4**	Tikkurila F497	МДФ · в цвет Tikkurila	полуглянц.	2	88	16,6 м
2. Ванная комната 5,57 м²	стены		**КМ2**	тон Paper F497 (тёплый белый)	плитка · аналог по хар.				22,3 м²
	потолок		**К5**	Tikkurila F497	Tikkurila · Luja 7	матовая	1	88	5,6 м²
	пол		**КМ3**	тон Castle J484 (тёплый песочный)	керамогранит · аналог по хар.				5,6 м²
3. Тёмная комната 2,96 м²	стены		**К1**	Tikkurila F497	Tikkurila · Optiva 5 Matt	матовая	2	88	16,9 м²
	потолок		**К3**	Tikkurila F497	Tikkurila · Anti-Reflex 2	глубокомат.	2	88	3,0 м²
	пол		**КМ1**	по образцу	инженерная доска · аналог по хар.				3,0 м²
	плинтус		**К4**	Tikkurila F497	МДФ · в цвет Tikkurila	полуглянц.	2	88	6,4 м
4. Детская 1 17,51 м²	стены		**К6**	Tikkurila F497	Tikkurila · Joker	полуматов.	2	88	40,1 м²
	потолок		**К3**	Tikkurila F497	Tikkurila · Anti-Reflex 2	глубокомат.	2	88	17,5 м²
	пол		**КМ1**	по образцу	инженерная доска · аналог по хар.				17,5 м²
	плинтус		**К4**	Tikkurila F497	МДФ · в цвет Tikkurila	полуглянц.	2	88	16,2 м
5. Коридор 4,54 м²	стены		**К7**	Tikkurila J484	Tikkurila · Optiva 20 Semimatt	полуматов.	2	55	22,2 м²
	потолок		**К3**	Tikkurila F497	Tikkurila · Anti-Reflex 2	глубокомат.	2	88	4,5 м²
	пол		**КМ4**	тон Claystone V486 (грейж)	керамогранит · аналог по хар.				4,5 м²
	плинтус		**К8**	Tikkurila J484	МДФ · в цвет Tikkurila	полуглянц.	2	55	8,1 м
6. Кухня 15,19 м²	стены		**К9**	Tikkurila F497	Tikkurila · Luja 7	полуматов.	1	88	34,5 м²
	потолок		**К5**	Tikkurila F497	Tikkurila · Luja 7	матовая	1	88	15,2 м²
	пол		**КМ1**	по образцу	инженерная доска · аналог по хар.				15,2 м²
	плинтус		**К4**	Tikkurila F497	МДФ · в цвет Tikkurila	полуглянц.	2	88	13,8 м
	фартук		**КМ5**	тон Paper F497 (тёплый белый)	керамогранит · аналог по хар.				1,1 м²

Схема палитры проекта

Стиль: Современный (контемпорари) · схема: аналоговая

основной	основной	второстепенный	акцентный
Tikkurila F497	**Tikkurila J484**	**Tikkurila V486**	**Tikkurila L481**
Paper LRV 88 стены 1,3,4,6,8,9,11,12,13; потолок 1,2,3,4,5,6,7,8,9,10,11,12,13; плинтус 1,3,4,6,8,9,11,12; текстиль/декор 1	Castle LRV 55 стены 5,7; плинтус 5,7; текстиль/декор 1,6	Claystone LRV 44 текстиль/декор 1,13	Silhouette LRV 18 акцент 1,11; текстиль/декор 1,11

План 60/30/10

60%	30%	10%

Окраска, факт — по площади стен, акцентов, потолков

94%	6%

окрашено всего 391,5 м²; второстепенный тон несут мебель и текстиль

Текстиль и декор в цветах вне палитры проекта

- NCS S 3005-Y20R тёплый тауп-серый — пом. 1 (Т3), 7 (Т15), 9 (Т18)
- Tikkurila H487 Pumice — пом. 1 (Т4), 4 (Т9, Т10, Т11), 9 (Т17, Т19)
- Tikkurila V484 Driftwood — пом. 4 (Т8), 9 (Т16), 13 (Т23)
- NCS S 5010-B10G серо-петроль — пом. 4 (Т12, Т13)
- Farrow & Ball No. 47 Green Smoke — пом. 9 (Т20, Т21)

Условные обозначения

- **К1** Tikkurila F497 · Paper · Optiva 5 Matt · матовая · кл. 2
- **К2** Tikkurila L481 · Silhouette · Optiva 5 Matt · матовая · кл. 2
- **К3** Tikkurila F497 · Paper · Anti-Reflex 2 · глубокомат. · кл. 2
- **К4** Tikkurila F497 · Paper · МДФ · полуглянц. · кл. 2
- **К5** Tikkurila F497 · Paper · Luja 7 · матовая · кл. 1
- **К6** Tikkurila F497 · Paper · Joker · полуматов. · кл. 2
- **К7** Tikkurila J484 · Castle · Optiva 20 Semimatt · полуматов. · кл. 2
- **К8** Tikkurila J484 · Castle · МДФ · полуглянц. · кл. 2
- **К9** Tikkurila F497 · Paper · Luja 7 · полуматов. · кл. 1
- дерево (доска, паркет, ламинат) — рисунок досок
- керамогранит, плитка, камень — сетка швов по формату

- **КМ1** инженерная доска · аналог: дуб натуральный брашированный, масло-воск, 14/4 мм
- **КМ2** плитка · аналог: керамогранит матовый, тон F497, 600×600×9 мм
- **КМ3** аналог: керамогранит матовый R10, тон J484, 600×600×10 мм
- **КМ4** аналог: керамогранит матовый R10, тон V486, 600×600×10 мм
- **КМ5** аналог: керамогранит матовый, тон F497, 600×600×9 мм
- **КМ6** аналог: керамогранит матовый R11, тон V486, 600×600×10 мм
- **КМ7** керамогранит · аналог: плинтус из керамогранита пола, подрезка 80 мм, верхняя кромка с запилом 45°

К — краска, КМ — отделочный материал (тон КМ — по описанию, эталон — образец материала); кл. — класс истирания (1 — самый стойкий к мытью); LRV — светлота цвета: 0 — чёрный, 100 — белый

Примечания

1. Цвет на листе и на экране — ориентир. До покраски — выкрас на объекте: не меньше А3 (или лист ГКЛ), на грунте под эту краску, не на белой шпаклёвке, в 2 слоя; на обороте — код, бренд, веер, дата. Смотреть днём и вечером, рядом с образцами пола и плитки. Красить только в цвет утверждённого выкраса.
2. Краску заказывать по коду из графы «Система и код цвета» у бренда этого кода, не «аналогом» другого; весь объём одного кода — одной партией, колеруемую краску — за один проход машины.
3. Площади — те же, что в ведомости отделки (лист С1); сколько краски заказать — в спецификации отделочных материалов (лист С4).
4. Колерная карта на 2 листах: обозначения — на каждом, схема и палитра — на первом, выкрасы — на последнем.

					Проект: Четырёхкомнатная квартира
	Лист	№ док.	Подпись	Дата	
Дизайнер	Кырлан А.С.			04.11.26	Колерная карта

Стадия	Лист	Листов
П	14	120

Колерная карта по помещениям (продолжение)

Помещение	Поверхность	Образец	Поз.	Система и код цвета	Производитель, линейка / материал, артикул	Блеск	Класс истирания	LRV	Площадь
7. Прихожая-коридор 7,8 м²	стены		**K7**	Tikkurila J484	Tikkurila · Optiva 20 Semimatt	полуматов.	2	55	23,8 м²
	потолок		**K3**	Tikkurila F497	Tikkurila · Anti-Reflex 2	глубокомат.	2	88	7,8 м²
	пол		**KM4**	тон Claystone V486 (грейж)	керамогранит · аналог по хар.				7,8 м²
	плинтус		**K8**	Tikkurila J484	МДФ · в цвет Tikkurila	полуглянц.	2	55	8,7 м
8. Гардеробная 2 1,29 м²	стены		**K1**	Tikkurila F497	Tikkurila · Optiva 5 Matt	матовая	2	88	8,7 м²
	потолок		**K3**	Tikkurila F497	Tikkurila · Anti-Reflex 2	глубокомат.	2	88	1,3 м²
	пол		**KM1**	по образцу	инженерная доска · аналог по хар.				1,3 м²
	плинтус		**K4**	Tikkurila F497	МДФ · в цвет Tikkurila	полуглянц.	2	88	3,3 м
9. Детская 2 10,96 м²	стены		**K6**	Tikkurila F497	Tikkurila · Joker	полуматов.	2	88	29,1 м²
	потолок		**K3**	Tikkurila F497	Tikkurila · Anti-Reflex 2	глубокомат.	2	88	11,0 м²
	пол		**KM1**	по образцу	инженерная доска · аналог по хар.				11,0 м²
	плинтус		**K4**	Tikkurila F497	МДФ · в цвет Tikkurila	полуглянц.	2	88	11,8 м
10. Санузел 1,31 м²	стены		**KM2**	тон Paper F497 (тёплый белый)	плитка · аналог по хар.				10,5 м²
	потолок		**K5**	Tikkurila F497	Tikkurila · Luja 7	матовая	1	88	1,3 м²
	пол		**KM3**	тон Castle J484 (тёплый песочный)	керамогранит · аналог по хар.				1,3 м²
11. Гостиная 14,55 м²	стены		**K1**	Tikkurila F497	Tikkurila · Optiva 5 Matt	матовая	2	88	27,8 м²
	акцент А		**K2**	Tikkurila L481	Tikkurila · Optiva 5 Matt	матовая	2	18	11,1 м²
	потолок		**K3**	Tikkurila F497	Tikkurila · Anti-Reflex 2	глубокомат.	2	88	14,6 м²
	пол		**KM1**	по образцу	инженерная доска · аналог по хар.				14,6 м²
	плинтус		**K4**	Tikkurila F497	МДФ · в цвет Tikkurila	полуглянц.	2	88	15,6 м
12. Гардеробная 1 2,83 м²	стены		**K1**	Tikkurila F497	Tikkurila · Optiva 5 Matt	матовая	2	88	15,0 м²
	потолок		**K3**	Tikkurila F497	Tikkurila · Anti-Reflex 2	глубокомат.	2	88	2,8 м²
	пол		**KM1**	по образцу	инженерная доска · аналог по хар.				2,8 м²
	плинтус		**K4**	Tikkurila F497	МДФ · в цвет Tikkurila	полуглянц.	2	88	5,5 м
13. Балкон 1 3,7 м²	стены		**K9**	Tikkurila F497	Tikkurila · Luja 7	полуматов.	1	88	16,5 м²
	потолок		**K5**	Tikkurila F497	Tikkurila · Luja 7	матовая	1	88	3,7 м²
	пол		**KM6**	тон Claystone V486 (грейж)	керамогранит · аналог по хар.				3,7 м²
	плинтус		**KM7**	тон Claystone V486 (грейж)	керамогранит · аналог по хар.				7,7 м

Условные обозначения

- **K1** Tikkurila F497 · Paper · Optiva 5 Matt · матовая · кл. 2
- **K2** Tikkurila L481 · Silhouette · Optiva 5 Matt · матовая · кл. 2
- **K3** Tikkurila F497 · Paper · Anti-Reflex 2 · глубокомат. · кл. 2
- **K4** Tikkurila F497 · Paper · МДФ · полуглянц. · кл. 2
- **K5** Tikkurila F497 · Paper · Luja 7 · матовая · кл. 1
- **K6** Tikkurila F497 · Paper · Joker · полуматов. · кл. 2
- **K7** Tikkurila J484 · Castle · Optiva 20 Semimatt · полуматов. · кл. 2
- **K8** Tikkurila J484 · Castle · МДФ · полуглянц. · кл. 2
- **K9** Tikkurila F497 · Paper · Luja 7 · полуматов. · кл. 1
- дерево (доска, паркет, ламинат) — рисунок досок
- керамогранит, плитка, камень — сетка швов по формату

- **KM1** инженерная доска · аналог: дуб натуральный брашированный, масло-воск, 14/4 мм
- **KM2** плитка · аналог: керамогранит матовый, тон F497, 600×600×9 мм
- **KM3** аналог: керамогранит матовый R10, тон J484, 600×600×10 мм
- **KM4** аналог: керамогранит матовый R10, тон V486, 600×600×10 мм
- **KM5** аналог: керамогранит матовый, тон F497, 600×600×9 мм
- **KM6** аналог: керамогранит матовый R11, тон V486, 600×600×10 мм
- **KM7** керамогранит · аналог: плинтус из керамогранита пола, подрезка 80 мм, верхняя кромка с запилом 45°

К — краска, КМ — отделочный материал (тон КМ — по описанию, эталон — образец материала); кл. — класс истирания (1 — самый стойкий к мытью); LRV — светлота цвета: 0 — чёрный, 100 — белый

Перечень выкрасов на согласование

№	Код	Бренд / веер	Пом. / стена	Подложка	Формат	Статус
1	F497	Tikkurila Symphony / Feel the Colour	1	ГКЛ, загрунтованный под эту краску	600×1000	на согласов.
2	G503	Tikkurila Symphony / Feel the Colour	1	ГКЛ, загрунтованный под эту краску	600×1000	на согласов.
3	G497	Tikkurila Symphony / Feel the Colour	1	ГКЛ, загрунтованный под эту краску	600×1000	на согласов.
4	L481	Tikkurila Symphony / Feel the Colour	1 A	ГКЛ, загрунтованный под эту краску	600×1000	на согласов.
5	V477	Tikkurila Symphony / Feel the Colour	1 A	ГКЛ, загрунтованный под эту краску	600×1000	на согласов.
6	L462	Tikkurila Symphony / Feel the Colour	1 A	ГКЛ, загрунтованный под эту краску	600×1000	на согласов.
7	J484	Tikkurila Symphony / Feel the Colour	5	ГКЛ, загрунтованный под эту краску	600×1000	на согласов.
8	X487	Tikkurila Symphony / Feel the Colour	5	ГКЛ, загрунтованный под эту краску	600×1000	на согласов.
9	X463	Tikkurila Symphony / Feel the Colour	5	ГКЛ, загрунтованный под эту краску	600×1000	на согласов.


… ещё 2 выкрасов — в ведомости отделки

Примечания

1. Цвет на листе и на экране — ориентир. До покраски — выкрас на объекте: не меньше А3 (или лист ГКЛ), на грунте под эту краску, не на белой шпаклёвке, в 2 слоя; на обороте — код, бренд, веер, дата. Смотреть днём и вечером, рядом с образцами пола и плитки. Красить только в цвет утверждённого выкраса.
2. Краску заказывать по коду из графы «Система и код цвета» у бренда этого кода, не «аналогом» другого; весь объём одного кода — одной партией, колеруемую краску — за один проход машины.
3. Площади — те же, что в ведомости отделки (лист С1); сколько краски заказать — в спецификации отделочных материалов (лист С4).
4. Колерная карта на 2 листах: обозначения — на каждом, схема и палитра — на первом, выкрасы — на последнем.

					Проект: Четырёхкомнатная квартира
	Лист	№ док.	Подпись	Дата	
Дизайнер	Кырлан А.С.			04.11.26	Колерная карта

Стадия	Лист	Листов
П	15	120

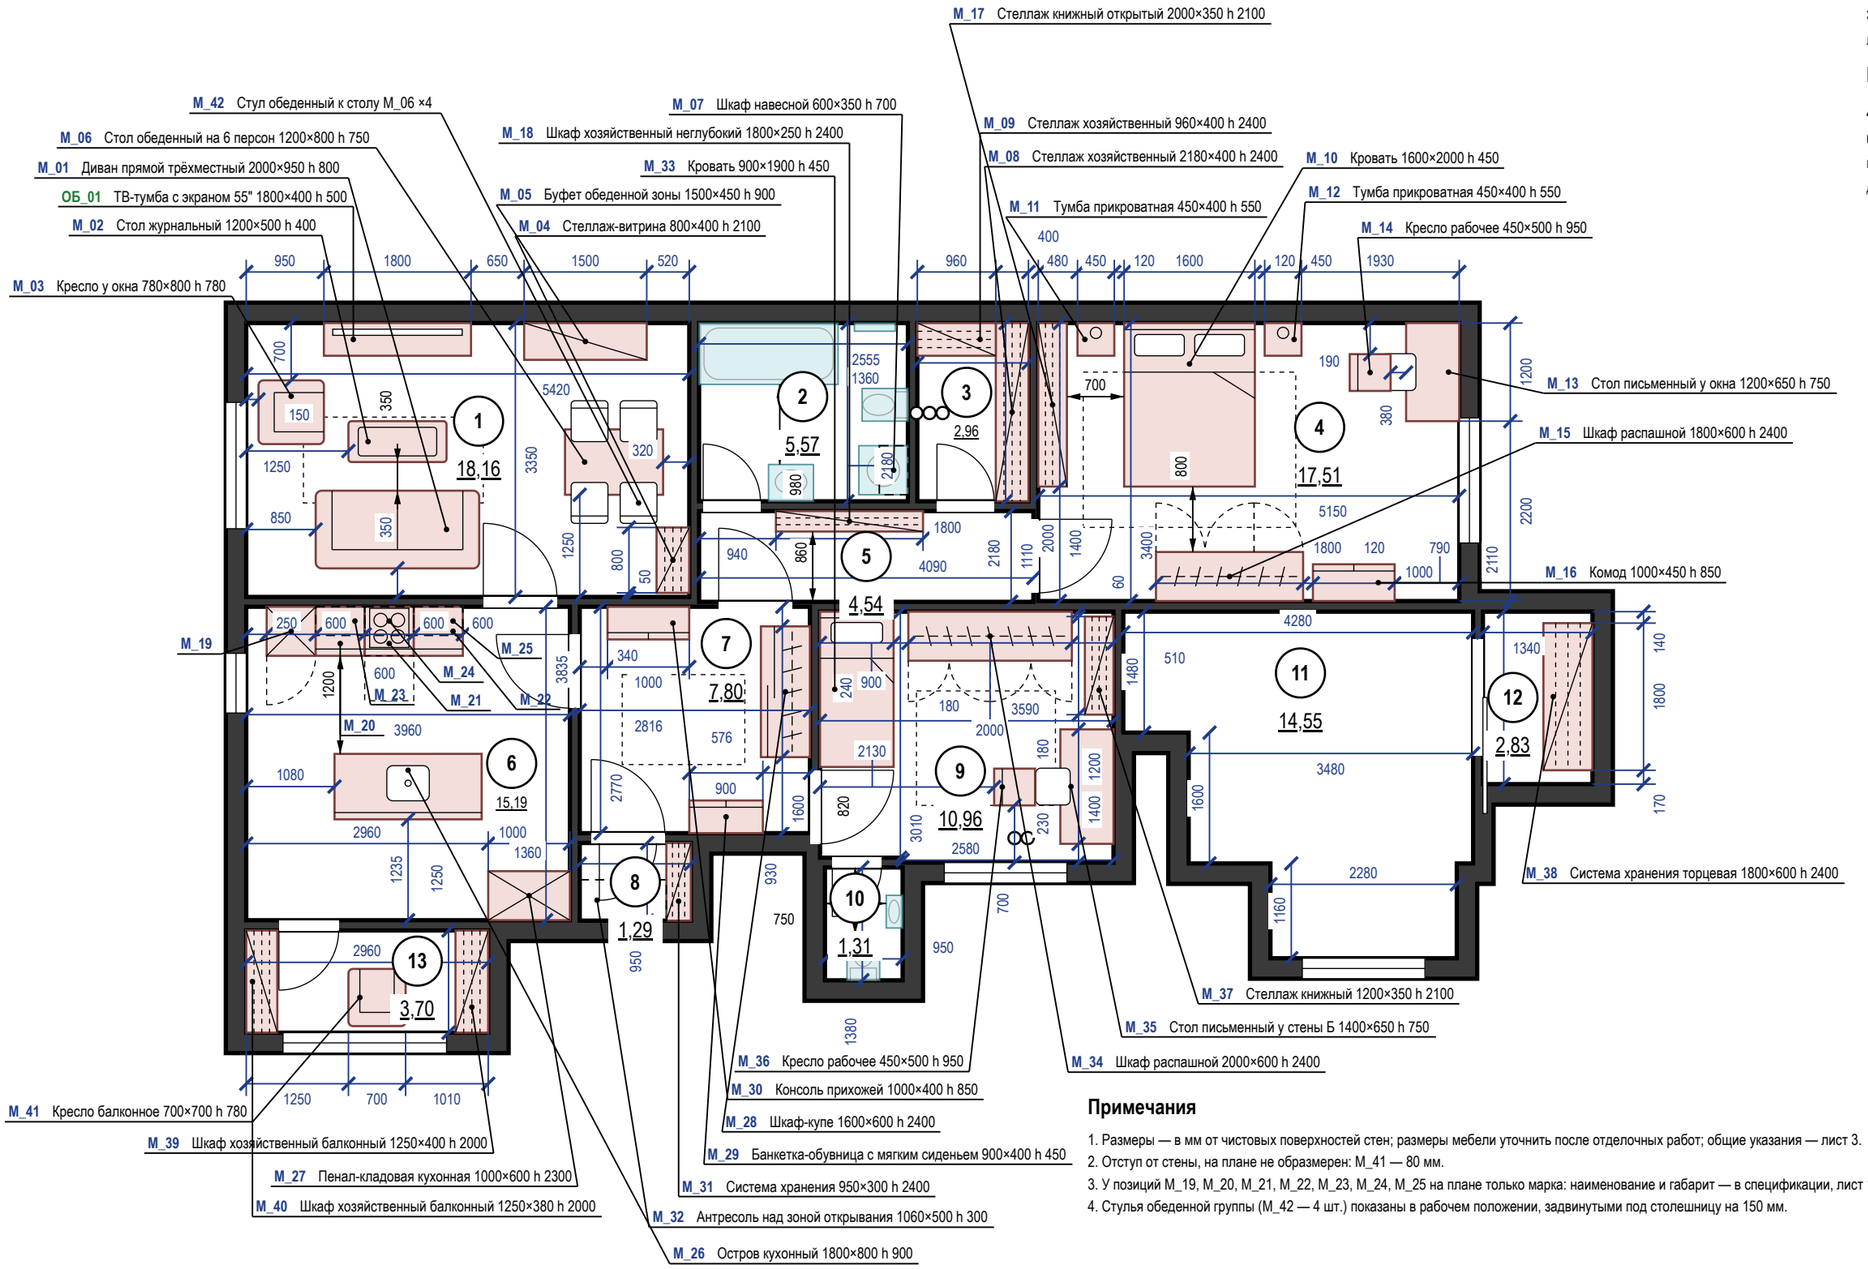

Экспликация помещений

лист 6 · на плане — номера в марках

Ведомость мебели и оборудования

43 позиц. (46 шт.) — не помещается на листе:
полностью на листе 17 «Спецификация мебели и оборудования»
марка, наименование, Ш×Г×В, материал, модель,
допуск замены. Марки на плане — по ней.

Примечания

1. Размеры — в мм от чистовых поверхностей стен; размеры мебели уточнить после отделочных работ; общие указания — лист 3.
2. Отступ от стены, на плане не образмерен: M_41 — 80 мм.
3. У позиций M_19, M_20, M_21, M_22, M_23, M_24, M_25 на плане только марка: наименование и габарит — в спецификации, лист 17.
4. Стулья обеденной группы (M_42 — 4 шт.) показаны в рабочем положении, задвинутыми под столешницу на 150 мм.

					Проект: Четырёхкомнатная квартира	**М 1:75**
	Лист	№ док.	Подпись	Дата		
Дизайнер	Кырлан А.С.			04.11.26	План размещения мебели и оборудования	Стадия: П; Лист: 16; Листов: 120

Поз.	Наименование и техническая характеристика	Тип, марка, обозначение документа, опросного листа	Код продукции	Поставщик	Ед. измерения	Кол.	Масса 1 ед., кг	Примечание
	Мебель встроенная и корпусная (изготовление по чертежам мебельщика)							
M_07	Шкаф навесной над стиральной машиной; каркас и полки — ЛДСП 16 мм, декор «дуб натуральный»; без фасадов; Ш×Г×В 600×350×700 мм			изготовление на заказ	шт.	1		пом. 2; крепление к стене
M_08	Стеллаж хозяйственный, 6 полок; каркас и полки — ЛДСП 16 мм, декор «дуб натуральный»; без фасадов; Ш×Г×В 2180×400×2400 мм			изготовление на заказ	шт.	1		пом. 3; крепление к стене
M_09	Стеллаж хозяйственный, 6 полок; каркас и полки — ЛДСП 16 мм, декор «дуб натуральный»; без фасадов; Ш×Г×В 960×400×2400 мм			изготовление на заказ	шт.	1		пом. 3; крепление к стене
M_15	Шкаф распашной, 3 секции; корпус ЛДСП 16 мм; фасады — МДФ 18 мм, эмаль матовая; цвет фасадов — в цвет стен (Tikkurila F497); Ш×Г×В 1800×600×2400 мм			изготовление на заказ	шт.	1		пом. 4; крепление к стене
M_17	Стеллаж книжный открытый; каркас и полки — ЛДСП 16 мм, декор «дуб натуральный»; без фасадов; Ш×Г×В 2000×350×2100 мм			изготовление на заказ	шт.	1		пом. 4; крепление к стене
M_18	Шкаф хозяйственный неглубокий; корпус ЛДСП 16 мм; фасады — МДФ 18 мм, эмаль матовая; цвет фасадов — в цвет стен (Tikkurila J484); Ш×Г×В 1800×250×2400 мм			изготовление на заказ	шт.	1		пом. 5; крепление к стене
M_19	Пенал кухонный с встроенным холодильником; корпус ЛДСП 16 мм; фасады — МДФ 18 мм, эмаль матовая; цвет фасадов в цвет стен (Tikkurila F497); Ш×Г×В 600×600×2300 мм			изготовление на заказ	шт.	1		пом. 6; крепление к стене
M_20	Модуль нижний, ящики; корпус ЛДСП 16 мм; фасады — МДФ 18 мм, эмаль матовая; цвет фасадов — в цвет стен (Tikkurila F497); Ш×Г×В 600×600×900 мм			изготовление на заказ	шт.	1		пом. 6
M_21	Модуль нижний: варочная панель и духовой шкаф; корпус ЛДСП 16 мм; фасады — МДФ 18 мм, эмаль матовая; цвет фасадов — в цвет стен (Tikkurila F497); Ш×Г×В 600×600×900 мм			изготовление на заказ	шт.	1		пом. 6
M_22	Модуль нижний, ящики и бутылочница; корпус ЛДСП 16 мм; фасады — МДФ 18 мм, эмаль матовая; цвет фасадов — в цвет стен (Tikkurila F497); Ш×Г×В 600×600×900 мм			изготовление на заказ	шт.	1		пом. 6
M_23	Модуль навесной, 2 секции; корпус ЛДСП 16 мм; фасады — МДФ 18 мм, эмаль матовая; цвет фасадов — в цвет стен (Tikkurila F497); Ш×Г×В 600×350×720 мм			изготовление на заказ	шт.	1		пом. 6
M_24	Вытяжка встраиваемая в шкаф; корпус ЛДСП 16 мм; фасады — МДФ 18 мм, эмаль матовая; цвет фасадов — в цвет стен (Tikkurila F497); Ш×Г×В 600×350×600 мм			изготовление на заказ	шт.	1		пом. 6
M_25	Модуль навесной, 2 секции; корпус ЛДСП 16 мм; фасады — МДФ 18 мм, эмаль матовая; цвет фасадов — в цвет стен (Tikkurila F497); Ш×Г×В 600×350×720 мм			изготовление на заказ	шт.	1		пом. 6
M_26	Остров кухонный с мойкой и посудомоечной машиной; корпус ЛДСП 16 мм; фасады — МДФ 18 мм, эмаль матовая; цвет фасадов — в цвет стен (Tikkurila F497); Ш×Г×В 1800×800×900 мм			изготовление на заказ	шт.	1		пом. 6
M_27	Пенал-кладовая кухонная; корпус ЛДСП 16 мм; фасады — МДФ 18 мм, эмаль матовая; цвет фасадов — в цвет стен (Tikkurila F497); Ш×Г×В 1000×600×2300 мм			изготовление на заказ	шт.	1		пом. 6; крепление к стене
M_28	Шкаф-купе, 3 двери; корпус ЛДСП 16 мм; фасады — ЛДСП 10 мм в алюминиевом профиле; Ш×Г×В 1600×600×2400 мм			изготовление на заказ	шт.	1		пом. 7; крепление к стене
M_31	Система хранения: штанга, полки, ящики; каркас и полки — ЛДСП 16 мм, декор «дуб натуральный»; без фасадов; Ш×Г×В 950×300×2400 мм			изготовление на заказ	шт.	1		пом. 8; крепление к стене
M_32	Антресоль над зоной открывания двери; каркас и полки — ЛДСП 16 мм, декор «дуб натуральный»; без фасадов; Ш×Г×В 1060×500×300 мм			изготовление на заказ	шт.	1		пом. 8; крепление к стене
M_34	Шкаф распашной, 4 секции; корпус ЛДСП 16 мм; фасады — МДФ 18 мм, эмаль матовая; цвет фасадов — в цвет стен (Tikkurila F497); Ш×Г×В 2000×600×2400 мм			изготовление на заказ	шт.	1		пом. 9; крепление к стене
M_38	Система хранения торцевая: штанги, полки; каркас и полки — ЛДСП 16 мм, декор «дуб натуральный»; без фасадов; Ш×Г×В 1800×600×2400 мм			изготовление на заказ	шт.	1		пом. 12; крепление к стене
M_39	Шкаф хозяйственный балконный; каркас и полки — ЛДСП 16 мм, декор «дуб натуральный»; без фасадов; Ш×Г×В 1250×400×2000 мм			изготовление на заказ	шт.	1		пом. 13; крепление к стене
M_40	Шкаф хозяйственный балконный; каркас и полки — ЛДСП 16 мм, декор «дуб натуральный»; без фасадов; Ш×Г×В 1250×380×2000 мм			изготовление на заказ	шт.	1		пом. 13; крепление к стене
	Мебель покупная							
M_01	Диван прямой трёхместный; обивка букле; Ш×Г×В 2000×950×800 мм	диван прямой, глубокая посадка, съёмные чехлы		аналог по характеристикам	шт.	1		пом. 1; допуск замены Ш 1900–2100, Г ≤ 1000

Примечания

1. Позиции мебели совпадают с марками на плане расстановки; размеры Ш×Г×В — Ш вдоль стены, Г от стены.
2. Размеры и привязки плана расстановки — в мм от чистовых поверхностей стен: слой штукатурки 20 мм по блоку и 5 мм шпаклёвки по ГКЛ учтён; привязки — от стен и углов помещения, а не от другой мебели.
3. План расстановки не является документацией для изготовления мебели. Встроенная и корпусная мебель изготавливается по чертежам мебельщика после контрольного обмера (после штукатурки); «стена в стену» — с зазором 10 мм с каждой стороны или с компенсаторами; графы «Тип, марка» и «Код продукции» для неё не заполняются (ГОСТ 21.110-2013).
4. Покупные изделия — аналог по характеристикам: заменять только на изделия не больше указанного габарита и того же материала и цвета.
5. Материал и цвет, не указанные в данных изделия, приняты по концепции: тон дерева — по полу, обивка — по вторичному цвету палитры; образцы согласовать до заказа.
6. Масса 1 ед. для изделий до 25 кг не указывается. Техника — по монтажным схемам изготовителя; выводы — по листам ЭОМ и ВК.

					Проект: Четырёхкомнатная квартира
	Лист	№ док.	Подпись	Дата	Спецификация мебели и оборудования
Дизайнер	Кырлан А.С.			04.11.26	

Стадия	Лист	Листов
П	17	120

Поз.	Наименование и техническая характеристика	Тип, марка, обозначение документа, опросного листа	Код продукции	Поставщик	Ед. измерения	Кол.	Масса 1 ед., кг	Примечание
М_02	Стол журнальный; дерево — дуб натуральный; Ш×Г×В 1200×500×400 мм	стол журнальный прямоугольный		аналог по характеристикам	шт.	1		пом. 1; допуск замены Ш 1100–1300
М_03	Кресло у окна; обивка — ткань, цвет Tikkurila V486; Ш×Г×В 780×800×780 мм	кресло мягкое на деревянных ножках		аналог по характеристикам	шт.	1		пом. 1; допуск замены Ш 750–850, В ≤ 790 (не выше подоконника)
М_04	Стеллаж-витрина; дерево — дуб натуральный, металл — латунь; Ш×Г×В 800×400×2100 мм	стеллаж открытый, 5 полок		аналог по характеристикам	шт.	1		пом. 1; крепление к стене; допуск замены Ш 750–850
М_05	Буфет обеденной зоны; дерево — дуб натуральный, металл — латунь; Ш×Г×В 1500×450×900 мм	буфет 3-дверный		аналог по характеристикам	шт.	1		пом. 1; крепление к стене; допуск замены Ш 1400–1600, Г ≤ 470
М_06	Стол обеденный на 6 персон; дерево — дуб натуральный; Ш×Г×В 1200×800×750 мм	стол обеденный прямоугольный, раскладной до 1800		аналог по характеристикам	шт.	1		пом. 1; допуск замены Ш 1200–1400 в сложенном виде, Г 800–900
М_42	Стул обеденный к столу М_06; обивка — ткань, цвет Tikkurila V486; каркас — дуб натуральный; Ш×Г×В 450×500×820 мм			аналог по характеристикам	шт.	4		пом. 1; замена ≤ габарита
ОБ_01	ТВ-тумба с экраном 55" диагональ 55"; крепление — настенный кронштейн по паспорту модели; Ш×Г×В 1800×400×500 мм	тумба ТВ подвесная, 3 ящика		аналог по характеристикам	шт.	1		пом. 1; допуск замены Ш 1700–1900, Г ≤ 450
М_10	Кровать 1600×2000; мягкое изголовье, обивка — ткань, цвет Tikkurila V486; Ш×Г×В 1600×2000×450 мм	кровать с мягким изголовьем		аналог по характеристикам	шт.	1		пом. 4; допуск замены Ш 1600, Д 2000–2050
М_11, М_12	Тумба прикроватная; дерево — дуб натуральный; Ш×Г×В 450×400×550 мм	тумба прикроватная, 2 ящика		аналог по характеристикам	шт.	2		пом. 4; допуск замены Ш 400–500
М_13	Стол письменный у окна; дерево — дуб натуральный, металл — чёрный матовый; Ш×Г×В 1200×650×750 мм	стол письменный с тумбой		аналог по характеристикам	шт.	1		пом. 4; допуск замены Ш 1100–1300, Г 600–700
М_14, М_36	Кресло рабочее; металл — чёрный матовый; Ш×Г×В 450×500×950 мм	кресло рабочее на роликах		аналог по характеристикам	шт.	2		пом. 4, 9; допуск замены Ш 480–560
М_16	Комод, 4 ящика; дерево — дуб натуральный; Ш×Г×В 1000×450×850 мм	комод 4 ящика		аналог по характеристикам	шт.	1		пом. 4; крепление к стене; допуск замены Ш 950–1100
М_29	Банкетка-обувница с мягким сиденьем; дерево — дуб натуральный; Ш×Г×В 900×400×450 мм	банкетка-обувница		аналог по характеристикам	шт.	1		пом. 7; допуск замены Ш 800–950
М_30	Консоль прихожей, 3 ящика; дерево — дуб натуральный, металл — чёрный матовый; Ш×Г×В 1000×400×850 мм	консоль-комод		аналог по характеристикам	шт.	1		пом. 7; крепление к стене; допуск замены Ш 950–1100
М_33	Кровать 900×1900; мягкое изголовье, обивка — ткань, цвет Tikkurila V486; Ш×Г×В 900×1900×450 мм	кровать односпальная с мягким изголовьем		аналог по характеристикам	шт.	1		пом. 9; допуск замены Ш 900, Д 1900–1950
М_35	Стол письменный у стены Б, рядом с окном стены В: свет боковой; дерево — дуб натуральный, металл — чёрный матовый; Ш×Г×В 1400×650×750 мм	стол письменный с тумбой		аналог по характеристикам	шт.	1		пом. 9; допуск замены Ш 1300–1500, Г 600–700
М_37	Стеллаж книжный; дерево — дуб натуральный; Ш×Г×В 1200×350×2100 мм			аналог по характеристикам	шт.	1		пом. 9; крепление к стене; замена ≤ габарита
М_41	Кресло балконное; металл — чёрный матовый; Ш×Г×В 700×700×780 мм	кресло на металлическом каркасе		аналог по характеристикам	шт.	1		пом. 13; допуск замены Ш 650–750, В ≤ 850 (не выше подоконника)
	Техника встраиваемая и бытовая (покупные изделия), светильники под розетки							
	Стиральная машина встраиваемая, у М_07	аналог по характеристикам: тип загрузки — по листу ВК, по листу ВК		по выбору заказчика до изготовления мебели	шт.	1		пом. 2; по схеме изготовителя
	Холодильник встраиваемый, в модуле М_19	аналог по характеристикам: полновстраиваемый под фасад, ниша 1780 × 560 × 550 мм, вентиляция решётка в цоколе, выход сверху		по выбору заказчика до изготовления мебели	шт.	1		пом. 6; по схеме изготовителя
	Духовой шкаф встраиваемый, в модуле М_21	аналог по характеристикам: 60 см, лицевая панель 595 мм, ниша 560 × 600, глубина ≥ 550 мм, вентиляция за прибором		по выбору заказчика до изготовления мебели	шт.	1		пом. 6; по схеме изготовителя

					Проект: Четырёхкомнатная квартира		
	Лист	№ док.	Подпись	Дата	Спецификация мебели и оборудования (продолжение)	Стадия	Лист	Листов
Дизайнер	Кырлан А.С.			04.11.26		П	18	120

Поз.	Наименование и техническая характеристика	Тип, марка, обозначение документа, опросного листа	Код продукции	Поставщик	Ед. измерения	Кол.	Масса 1 ед., кг	Примечание
	Варочная панель встраиваемая, индукционная, в модуле M_21	аналог по характеристикам: индукционная 60 см, вырез 560 × 490 мм по шаблону модели		по выбору заказчика до изготовления мебели	шт.	1		пом. 6; по схеме изготовителя
	Вытяжка встраиваемая, в модуле M_24	аналог по характеристикам: производительность — по расчёту ОВ, шум ≤ 55 дБ(А)		по выбору заказчика до изготовления мебели	шт.	1		пом. 6; по схеме изготовителя
	Посудомоечная машина встраиваемая, в модуле M_26; ниша 600 мм	аналог по характеристикам: полновстраиваемая 60 см под фасад, ниша 600 × по высоте ряда мм, навеска фасада в комплекте		по выбору заказчика до изготовления мебели	шт.	1		пом. 6; по схеме изготовителя
	Торшер, у поз. M_01; абажур — ткань или опаловое стекло; лампа 2700 K			аналог по характеристикам	шт.	1		пом. 1; розетка Р3 (ЭОМ)
	Текстиль							
T1	Портьеры-волна, два полотна; лён 100 %; цвет Tikkurila V486; карниз 2150 мм, высота 2690 мм, сборка 2			аналог по характеристикам	шт.	2		пом. 1
T2	Тюль-вуаль, одно полотно; полиэстер 100 %; цвет Tikkurila F497; карниз 2150 мм, высота 2690 мм, сборка 2,5			аналог по характеристикам	шт.	1		пом. 1
T3	Ковёр мягкой группы; шерсть 100 %; цвет NCS S 3005-Y20R; 2200×1050 мм			аналог по характеристикам	шт.	1		пом. 1; с подложкой
T4	Подушки декоративные на диван; лён 100 %; цвет Tikkurila H487			аналог по характеристикам	шт.	3		пом. 1
T5	Подушки декоративные на диван, акцент; хлопковый бархат 100 %; цвет Tikkurila L481			аналог по характеристикам	шт.	2		пом. 1
T6	Плед на диван; шерсть мериноса 100 %; цвет Tikkurila L481			аналог по характеристикам	шт.	1		пом. 1
T7	Раннер на обеденный стол; лён 100 %; цвет Tikkurila J484			аналог по характеристикам	шт.	1		пом. 1
T8	Портьеры стационарные, два полотна; лён 55 %, хлопок 45 %; цвет Tikkurila V484; карниз 2140 мм, высота 2690 мм, сборка 2			аналог по характеристикам	шт.	2		пом. 4
T9	Римская штора блэкаут: окно закрывает она, стол M_13 у окна не мешает; хлопок 100 %, подкладка полиэстер; цвет Tikkurila H487; карниз 1650 мм, высота 1900 мм			аналог по характеристикам	шт.	1		пом. 4
T10	Ковёр у кровати; шерсть 80 %, хлопок 20 %; цвет Tikkurila H487; 2600×1900 мм			аналог по характеристикам	шт.	1		пом. 4; с подложкой
T11	Подушки декоративные на кровать; лён 100 %; цвет Tikkurila H487			аналог по характеристикам	шт.	2		пом. 4
T12	Подушка декоративная, акцент; хлопковый бархат 100 %; цвет NCS S 5010-B10G			аналог по характеристикам	шт.	1		пом. 4
T13	Плед на кровать; хлопок 100 %; цвет NCS S 5010-B10G			аналог по характеристикам	шт.	1		пом. 4
T14	Рулонная штора кассетная, ткань димаут; полиэстер 100 %; цвет Tikkurila J484; карниз 890 мм, высота 1900 мм			аналог по характеристикам	шт.	1		пом. 6
T15	Ковёр прихожей, низкий ворс; шерсть 80 %, полиамид 20 %; цвет NCS S 3005-Y20R; 1500×1100 мм			аналог по характеристикам	шт.	1		пом. 7; с подложкой
T16	Портьеры стационарные, два полотна, до подоконника: радиатор под окном открыт; лён 55 %, хлопок 45 %; цвет Tikkurila V484; карниз 1800 мм, высота 1930 мм, сборка 2			аналог по характеристикам	шт.	2		пом. 9
T17	Римская штора блэкаут: закрывает проём целиком, радиатор под окном не задевает; хлопок 100 %, подкладка полиэстер; цвет Tikkurila H487; карниз 1620 мм, высота 1900 мм			аналог по характеристикам	шт.	1		пом. 9
T18	Ковёр игровой зоны; шерсть 100 %; цвет NCS S 3005-Y20R; 1700×1400 мм			аналог по характеристикам	шт.	1		пом. 9; с подложкой
T19	Подушки декоративные на кровать; лён 100 %; цвет Tikkurila H487			аналог по характеристикам	шт.	2		пом. 9
T20	Подушка декоративная, акцент; шерсть 60 %, полиэстер 40 %; цвет Farrow & Ball No. 47			аналог по характеристикам	шт.	1		пом. 9
T21	Плед на кровать; хлопок 100 %; цвет Farrow & Ball No. 47			аналог по характеристикам	шт.	1		пом. 9
T22	Рулонная штора кассетная, солнцезащитная; полиэстер 100 %; цвет Tikkurila V486; карниз 2140 мм, высота 1700 мм			аналог по характеристикам	шт.	1		пом. 13
T23	Плед на кресло M_41; шерсть 100 %; цвет Tikkurila V484			аналог по характеристикам	шт.	1		пом. 13

					Проект: Четырёхкомнатная квартира		
	Лист	№ док.	Подпись	Дата	Спецификация мебели и оборудования (продолжение)	Стадия	Лист	Листов
Дизайнер	Кырлан А.С.			04.11.26		П	19	120

Поз.	Наименование и техническая характеристика	Тип, марка, обозначение документа, опросного листа	Код продукции	Поставщик	Ед. измерения	Кол.	Масса 1 ед., кг	Примечание
	Декор							
ДК1	Картина над диваном: крупная абстракция, холст, тонкая рама; 1400×900 мм; низ на 1000 мм от пола			аналог по характеристикам	шт.	1	6	пом. 1; крепление: планка на дюбелях, 4 точки
ДК2	Зеркало над буфетом, рама шпон дуба; 1000×800 мм; низ на 1100 мм от пола			аналог по характеристикам	шт.	1	12	пом. 1; крепление: анкер химический, 4 точки
ДК3	Фикус лировидный в кашпо Ø400; 450×450 мм			аналог по характеристикам	шт.	1		пом. 1
ДК4	Зеркало над раковиной C_03, влагостойкое; 600×800 мм; низ на 1100 мм от пола			аналог по характеристикам	шт.	1	5	пом. 2; крепление: зеркалодержатели, 4 точки
ДК5	Картина над изголовьем: графика, паспарту, рама; 1100×700 мм; низ на 1300 мм от пола			аналог по характеристикам	шт.	1	4	пом. 4; крепление: две петли на дюбелях
ДК6	Зеркало над комодом M_16; 700×900 мм; низ на 1050 мм от пола			аналог по характеристикам	шт.	1	8	пом. 4; крепление: анкер химический, 4 точки
ДК7	Хлорофитум хохлатый в напольном кашпо Ø380; 420×420 мм			аналог по характеристикам	шт.	1		пом. 4
ДК8	Часы настенные Ø400; 400×400 мм; центр на 1550 мм от пола			аналог по характеристикам	шт.	1	2	пом. 6; крепление: дюбель с крюком, 1 точка
ДК9	Хлорофитум хохлатый на подоконнике (отм. +0,800); 300×200 мм; низ на 800 мм от пола			аналог по характеристикам	шт.	1		пом. 6
ДК10	Зеркало над консолью M_30; 700×1000 мм; низ на 1050 мм от пола			аналог по характеристикам	шт.	1	9	пом. 7; крепление: анкер химический, 4 точки
ДК11	Замиокулькас в напольном кашпо Ø360; 400×400 мм			аналог по характеристикам	шт.	1		пом. 7
ДК12	Картина над изголовьем: графика, паспарту, рама; 600×800 мм; низ на 1200 мм от пола			аналог по характеристикам	шт.	1	3	пом. 9; крепление: две петли на дюбелях
ДК13	Постер в раме, левый (группа «постеры»); 400×500 мм; низ на 1250 мм от пола			аналог по характеристикам	шт.	1	2	пом. 9; крепление: петля на дюбеле
ДК14	Постер в раме, средний (группа «постеры»); 400×500 мм; низ на 1250 мм от пола			аналог по характеристикам	шт.	1	2	пом. 9; крепление: петля на дюбеле
ДК15	Постер в раме, правый (группа «постеры»); 400×500 мм; низ на 1250 мм от пола			аналог по характеристикам	шт.	1	2	пом. 9; крепление: петля на дюбеле
ДК16	Спатифиллум в напольном кашпо Ø360; 400×400 мм			аналог по характеристикам	шт.	1		пом. 9
ДК17	Зеркало над раковиной C_07, влагостойкое; 500×700 мм; низ на 1150 мм от пола			аналог по характеристикам	шт.	1	4	пом. 10; крепление: зеркалодержатели, 4 точки
ДК20	Картина: тёмная лиловая абстракция, холст, тонкая рама; 800×600 мм; низ на 1300 мм от пола			аналог по характеристикам	шт.	1	4	пом. 11; крепление: планка на дюбелях, 2 точки
ДК21	Ваза напольная, керамика матовая; 300×300 мм			аналог по характеристикам	шт.	1		пом. 11
ДК18	Зеркало ростовое 500×1600; 500×1600 мм; низ на 250 мм от пола			аналог по характеристикам	шт.	1	12	пом. 12; крепление: анкер химический, 4 точки + опора снизу
ДК19	Лавр благородный в напольном кашпо Ø380; 400×400 мм			аналог по характеристикам	шт.	1		пом. 13

					Проект: Четырёхкомнатная квартира		
	Лист	№ док.	Подпись	Дата	Спецификация мебели и оборудования (продолжение)	Стадия	Лист	Листов
Дизайнер	Кырлан А.С.			04.11.26		П	20	120

Ведомость изделий

Марка	Наименование	Пом.	Ш×Г×В, мм	Корпус	Фасад	Кромка, мм	Кол.
M_07	Система хранения	2	600×350×700	ЛДСП 16	без фасадов	0,4 / 2	1
M_08	Система хранения	3	2180×400×2400	ЛДСП 16	без фасадов	0,4 / 2	1
M_09	Система хранения	3	960×400×2400	ЛДСП 16	без фасадов	0,4 / 2	1
M_15	Шкаф распашной	4	1800×600×2400	ЛДСП 16	МДФ 18 мм, эмаль матовая	0,4 / 2	1
M_17	Система хранения	4	2000×350×2100	ЛДСП 16	без фасадов	0,4 / 2	1
M_18	Система хранения	5	1800×250×2400	ЛДСП 16	МДФ 18 мм, эмаль матовая	0,4 / 2	1
M_28	Шкаф-купе	7	1600×600×2400	ЛДСП 16	ЛДСП 10 мм в алюминиевом профиле	0,4 / 2	1
M_31	Система хранения	8	950×300×2400	ЛДСП 16	без фасадов	0,4 / 2	1
M_32	Система хранения	8	1060×500×300	ЛДСП 16	без фасадов	0,4 / 2	1
M_34	Шкаф распашной	9	2000×600×2400	ЛДСП 16	МДФ 18 мм, эмаль матовая	0,4 / 2	1
M_38	Система хранения	12	1800×600×2400	ЛДСП 16	без фасадов	0,4 / 2	1
M_39	Система хранения	13	1250×400×2000	ЛДСП 16	без фасадов	0,4 / 2	1
M_40	Система хранения	13	1250×380×2000	ЛДСП 16	без фасадов	0,4 / 2	1
M_19	Пенал: холодильник встр.	6	600×600×2300	ЛДСП 16	МДФ 18 мм, эмаль матовая	0,4 / 2	1
M_20	Модуль нижний: ящики	6	600×600×900	ЛДСП 16	МДФ 18 мм, эмаль матовая	0,4 / 2	1
M_23	Модуль навесной: полки	6	600×350×720	ЛДСП 16	МДФ 18 мм, эмаль матовая	0,4 / 2	1
M_21	Модуль нижний: духовой шкаф, варочная	6	600×600×900	ЛДСП 16	МДФ 18 мм, эмаль матовая	0,4 / 2	1
M_24	Модуль навесной: полки	6	600×350×600	ЛДСП 16	МДФ 18 мм, эмаль матовая	0,4 / 2	1
M_22	Модуль нижний: ящики	6	600×600×900	ЛДСП 16	МДФ 18 мм, эмаль матовая	0,4 / 2	1
M_25	Модуль навесной: полки	6	600×350×720	ЛДСП 16	МДФ 18 мм, эмаль матовая	0,4 / 2	1
M_27	Пенал: полки	6	1000×600×2300	ЛДСП 16	МДФ 18 мм, эмаль матовая	0,4 / 2	1
M_26	Остров (M_26.1, M_26.2, M_26.3)	6	1800×800×900	ЛДСП 16	МДФ 18 мм, эмаль матовая	0,4 / 2	1

Ведомость встраиваемой техники

Поз.	Прибор	Ниша, вырез, мм	Вентиляция	Питание	Схема
M_19	Холодильник встраиваемый, ниша 1780	ниша 1780 × 560 × 550	решётка в цоколе, канал за корпусом, выход сверху	Р20: M_20, H=150 — в соседнем модуле, за ящиком	по модели
M_21	Духовой шкаф встраиваемый, 60 см	ниша 560 × 600, глубина ≥ 550	зазор за шкафом, вырез в задней стенке	ЭВ4: M_22, H=150 — в соседнем модуле, за ящиком	по модели
M_21	Варочная панель индукционная, 60 см	вырез в столешнице 560 × 490		ЭВ3: M_20, H=150 — в соседнем модуле, за ящиком	по модели
M_24	Вытяжка встраиваемая в навесной модуль, 60 см	низ ≥ 650 над панелью	воздуховод к вентканалу, короб до потолка	Р21: M_24, H=2200 — в навесном модуле	по модели
M_26.2	Мойка врезная / подстольная с сифоном	вырез по шаблону, ориентир 760 × 480		смеситель — выводы ВК	по модели

Ведомость фурнитуры

№	Фурнитура	Тип, размер	Изделия	Кол.
1	Полкодержатель с фиксацией	ø5 мм	M_07, M_08, M_09, M_15, M_17, M_18, M_28, M_31, M_34, M_38, M_39, M_40, M_19, M_23, M_24, M_25, M_27	328
2	Анкер по основанию стены	по таблице крепежа	M_07, M_08, M_09, M_15, M_17, M_18, M_28, M_31, M_32, M_34, M_38, M_39, M_40, M_23, M_24, M_25	95
3	Уголок крепления к стене от опрокидывания	стальной	M_07, M_08, M_09, M_15, M_17, M_18, M_28, M_31, M_32, M_34, M_38, M_39, M_40, M_19, M_27	30
4	Штанга выдвижная торцевая	L по глубине	M_08, M_09, M_17, M_39, M_40	9
5	Опора регулируемая с цоколем на клипсах	ход 20 мм	M_08, M_09, M_15, M_17, M_18, M_28, M_31, M_34, M_38, M_39, M_40	78
6	Петля накладная 110° с доводчиком	чашка 35 мм	M_15, M_18, M_34, M_19, M_23, M_24, M_25, M_27, M_26	100
7	Штанга овальная 30×15, L = 876	+ 2 держателя	M_15	1
8	Система дверей купе: профиль, направляющие, ролики	на 2 двери	M_28	1
9	Ручка-профиль вертикальная	в цвет профиля	M_28	2
10	Штанга овальная 30×15, L = 776	+ 2 держателя	M_28	1
11	Полка для обуви выдвижная наклонная	ширина 776	M_28	3
12	Штанга овальная 30×15, L = 976	+ 2 держателя	M_34	1
13	Штанга овальная 30×15, L = 579	+ 2 держателя	M_38	3
14	Ручка-профиль	латунь матовая	M_19, M_20, M_23, M_21, M_24, M_22, M_25, M_27, M_26	26
15	Опора кухонная регулируемая 100–120 мм	+ клипса цоколя	M_19, M_20, M_21, M_22, M_27, M_26	34
16	Направляющие полного выдвижения с доводчиком NL 500	пара	M_20, M_21, M_22, M_26	13
17	Навес регулируемый для навесного шкафа	пара на секцию	M_23, M_24, M_25	3
18	Шина монтажная	L = 540	M_23, M_24, M_25	3
19	Уголок крепления острова к полу	стальной, в цоколе	M_26	4


Примечания

1. Модели техники выбирает заказчик до изготовления мебели; ниши, вырезы и вентиляция — по монтажной схеме выбранной модели (условие гарантии), её номер вносится в ведомость.
2. Количество фурнитуры — по чертежам изделий; запас крепежа 5 %. Аналоги — по характеристикам (доводчик, нагрузка, ход).
3. Цвет корпусов, фасадов и профилей — по колерной карте проекта. Кромка — скрытые / видимые торцы, мм.


					Проект: Четырёхкомнатная квартира
	Лист	№ док.	Подпись	Дата	
Дизайнер	Кырлан А.С.			04.11.26	Ведомости изделий, техники и фурнитуры

Стадия	Лист	Листов
П	21	120


Фрагмент 1. Ванная комната (пом. 2)

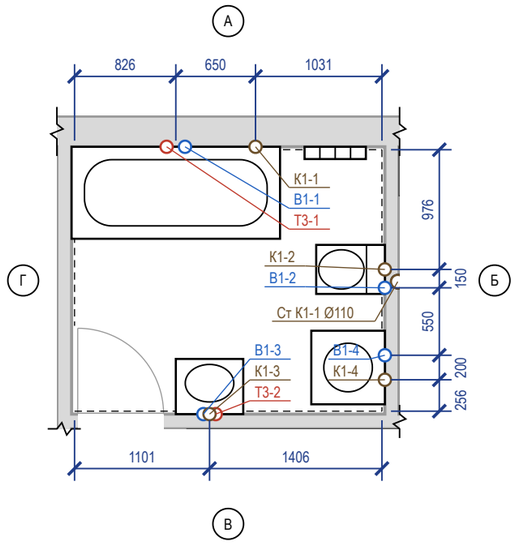

Фрагмент 2. Кухня (пом. 6)

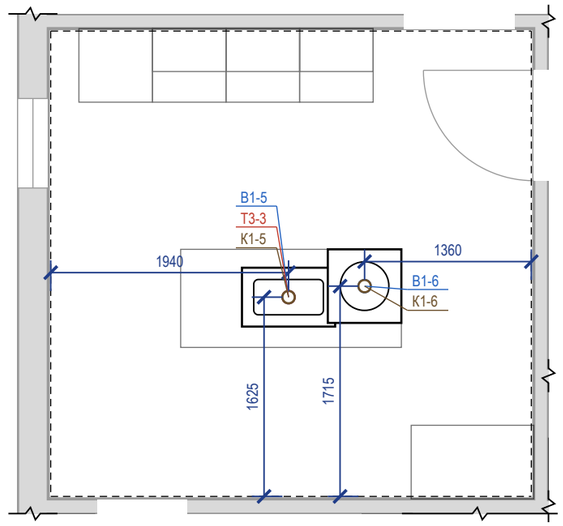

Фрагмент 3. Санузел (пом. 10)

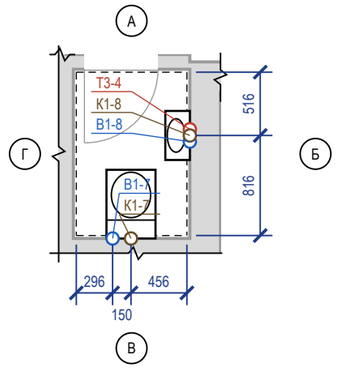

Ведомость привязок выводов

Код	Прибор	Ø	H, мм	Привязка от чист. стен, мм	Прим.
В1-1	С_01 ванна	½"	800	ст. А: 901 от Г	межос. 150
Т3-1	С_01 ванна	½"	800	ст. А: 751 от Г	межос. 150
К1-1	С_01 ванна	Ø50	60	ст. А: 1031 от Б	
В1-2	С_02 унитаз подвесной	½"	250	ст. Б: 1006 от В	в раме инсталляции
К1-2	С_02 унитаз подвесной	Ø110	220	ст. Б: 976 от А	
В1-3	С_03 умывальник	½"	550	ст. В: 1051 от Г	межос. 100
Т3-2	С_03 умывальник	½"	550	ст. В: 1151 от Г	межос. 100
К1-3	С_03 умывальник	Ø40	450	ст. В: 1101 от Г	
В1-4	ОБ_02 стиральная машина	½"	700	ст. Б: 456 от В	кран машины
К1-4	ОБ_02 стиральная машина	Ø40	700	ст. Б: 256 от В	
В1-5	С_05 мойка кухонная	½"	600	1940 от Г; 1625 от В	межос. 100
Т3-3	С_05 мойка кухонная	½"	600	1940 от Г; 1625 от В	межос. 100
К1-5	С_05 мойка кухонная	Ø50	400	1940 от Г; 1625 от В	
В1-6	ОБ_03 посудомоечная машина	½"	550	1360 от Б; 1715 от В	кран ПММ
К1-6	ОБ_03 посудомоечная машина	Ø50	550	1360 от Б; 1715 от В	
В1-7	С_06 унитаз подвесной	½"	250	ст. В: 296 от Г	в раме инсталляции
К1-7	С_06 унитаз подвесной	Ø110	220	ст. В: 446 от Г	
В1-8	С_07 умывальник	½"	550	ст. Б: 566 от А	межос. 100
Т3-4	С_07 умывальник	½"	550	ст. Б: 466 от А	межос. 100
К1-8	С_07 умывальник	Ø40	450	ст. Б: 516 от А	

Условные обозначения


- вывод В1 (код — в ведомости привязок)
- вывод Т3 (код — в ведомости привязок)
- вывод К1 (код — в ведомости привязок)
- сантехприбор по расстановке (габарит модели)
- чистовая поверхность стены (от неё привязки)
- стояк «Ст К1-N / Ст В1-N» (ГОСТ 21.601), Ø мм
- стояк Т3 не на обмере — принят в шахте рядом со Ст В1, сверить
- линия обрыва (граница фрагмента)
- А — обозначение стены А–Г (как на развёртках)

Примечания


1. Привязки выводов даны от чистовых поверхностей стен (облицовка на сторону: ванная комната — 24 мм (штукатурка 10 + клей 5 + плитка 9); кухня — 20 мм (по данным); санузел — 24 мм (штукатурка 10 + клей 5 + плитка 9)); эти же грани — на развёртках и в раскладке плитки. Высоты — от чистого пола помещения.
2. До черновой разводки сверить по паспорту выбранного прибора (смеситель, инсталляция, сифон).
3. Горячая вода (Т3) — слева от холодной (В1), если смотреть на прибор. Допуск установки выводов: ±5 мм в группе, ±20 мм у отдельно стоящих.
4. Расчёт систем водоснабжения и канализации и подбор оборудования выполняет проектная организация; лист задаёт места и высоты выводов.
5. С_05 мойка кухонная (В1-5, Т3-3, К1-5) — выводы в полу: пирог пола 170 мм их не укрывает (нужно 307 мм, расчёт — профиль К1 схемы разводки); до решения заказчика (подъём пола или другой смеситель / выпуск) не выполнять.
6. ОБ_03 посудомоечная машина (В1-6, К1-6) — выводы в полу: пирог пола 170 мм их не укрывает (нужно 257 мм, расчёт — профиль К1 схемы разводки); до решения заказчика (подъём пола или другой смеситель / выпуск) не выполнять.
7. Ст Т3-2 на обмере не показаны: приняты рядом с Ст В1-2 (в МКД стоят группой); положение сверить на объекте до разметки.
8. Стояки в коробах/шахтах не замоноличивать; стояк К1 в коробе — звукоизоляция стояка в коробе без жёсткого контакта с трубой; к арматуре и ревизиям — люк не меньше 300×400.
9. Штриховая линия чистовой грани стены прерывается на длине полотна открытой двери, лежащего вдоль грани (линии не должны сливаться при печати); положение грани — по размерам, а не по штриху.

					Проект: Четырёхкомнатная квартира	М 1:50
	Лист	№ док.	Подпись	Дата		
Дизайнер	Кырлан А.С.			04.11.26	План выводов сантехники	Стадия: П; Лист: 22; Листов: 120


План квартиры (М 1:400)

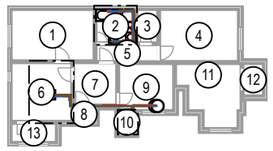


Фр. 1. Ванная комната (М 1:40)

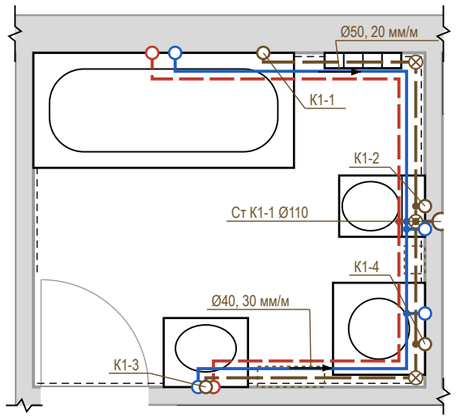

Фр. 2. Кухня (М 1:40)

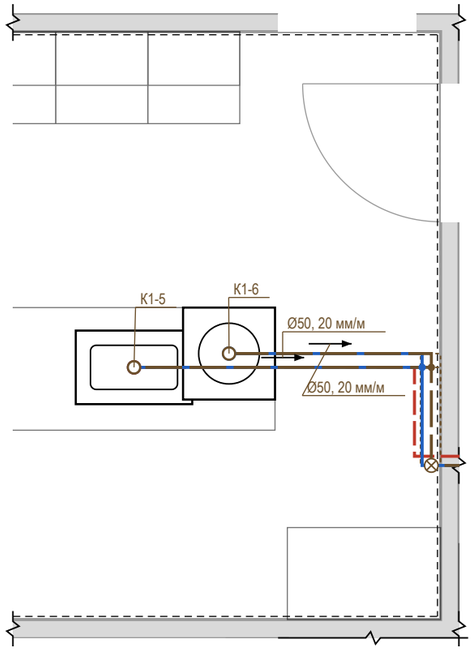

Фр. 3. Санузел (М 1:40)

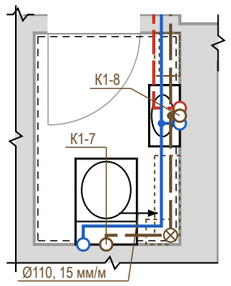

Условные обозначения


- В1 — водопровод хозяйственно-питьевой (ХВС), PP-R Ø20
- Т3 — горячее водоснабжение, подача (ГВС), PP-R Ø20
- К1 — канализация бытовая
- направление уклона К1 / пола: Ø, мм на 1 м
- ⊗ ревизия (прочистка) К1 — доступ сохранить
- • тройник (ответвление к прибору)
- короб К1 над чистым полом (ГКЛВ под плитку)
- ○ вывод В1 (код — в ведомости привязок)
- ○ вывод Т3 (код — в ведомости привязок)
- ○ вывод К1 (код — в ведомости привязок)
- ▭ сантехприбор по расстановке (габарит модели)
- ○ стояк «Ст К1-N / Ст В1-N» (ГОСТ 21.601), Ø мм
- ◌ стояк Т3 не на обмере — принят в шахте рядом со Ст В1, сверить
- ⌇ линия обрыва (граница фрагмента)
- ▭ граница фрагмента на плане (Фр. N)

Профиль выпусков К1 (до врезки в стояк)

Выпуск	Прибор	Ø	L, м	i, мм/м	Δh, мм	Прокладка, мм
К1-7	С_06 унитаз подвесной	Ø110	3,60	15	54	короб 200×140
К1-2	С_02 унитаз подвесной	Ø110	0,35	20	7	над полом за приборами
К1-5	С_05 мойка кухонная	Ø50	10,10	20	202	в полу не помещается: 307 > 170; до решения
К1-6	ОБ_03 посудомоечная машина	Ø50	7,60	20	152	в полу не помещается: 257 > 170; до решения
К1-1	С_01 ванна	Ø50	2,30	20	46	в полу, стяжка ≥ 151
К1-3	С_03 умывальник	Ø40	2,65	30	80	короб 150×110
К1-8	С_07 умывальник	Ø40	2,50	30	75	короб 150×110
К1-4	ОБ_02 стиральная машина	Ø40	1,05	30	32	в полу, стяжка ≥ 127

Короб h×b: h — от чистого пола, b — от чистовой стены. Стяжка 155 мм — лист полов.

Узел ввода В1, Т3 (схема, без масштаба)

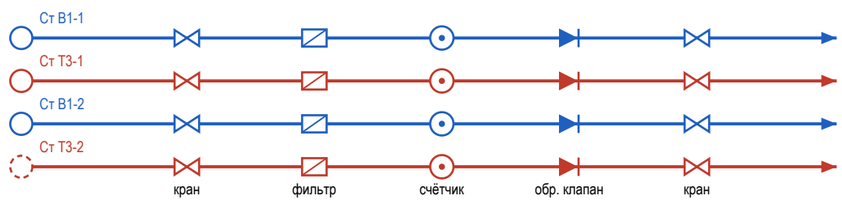

состав узла — по согласованию

⊗ Ст К1-1, Ст К1-2: ревизия на стояке — люк в коробе


Примечания

1. Трассы принципиальные, построены от стояков вдоль стен помещений; фактическое положение фиксируется исполнительной схемой с привязками (фото с рулеткой) до закрытия.
2. Уклон К1 не менее 1/d и не более 150 мм/м (СП 30.13330.2020, п. 19.1), приняты практические уклоны; поворот — двумя отводами 45°, ревизия после поворота, доступ сохранить. Стояк К1 в коробе — звукоизоляция стояка в коробе, без жёсткого контакта короба с трубой.
3. Решение по К1: стяжка 155 мм не укрывает трубы (нужно Ø + Δh + 45 мм) — выпуски идут над чистым полом вдоль стен: К1-2 — за приборами и в раме инсталляции; К1-7, К1-3, К1-8 — в коробе ГКЛВ под плитку (размеры в профиле). Короба — на развёртках; отметку низа врезки в стояк замерить до черновых работ.
4. К1-5 (С_05 мойка кухонная, выпуск в пол): Δh 202 + Ø50 + 45 = 307 мм > пирога 170 мм — в стяжке не помещается, в короб не уходит: подиум или подъём пола на 140 мм или прибор ближе к стояку — решение заказчика; до решения не выполнять.
5. К1-6 (ОБ_03 посудомоечная машина, выпуск в пол): Δh 152 + Ø50 + 45 = 257 мм > пирога 170 мм — в стяжке не помещается, в короб не уходит: подиум или подъём пола на 90 мм или прибор ближе к стояку — решение заказчика; до решения не выполнять.
6. Состав узла ввода В1, Т3 — по согласованию: на схеме типовой узел — кран шаровой, фильтр, счётчик, обратный клапан, кран; состав и места не определены (записи реестра нет). Доступ к арматуре — через люк не меньше 300×400. Водопровод — в штробе стен или в коробах; трубы испытать давлением до закрытия (акт скрытых работ).
7. Расчёт систем, диаметры магистралей и подбор оборудования выполняет проектная организация; врезка и перенос стояков — по согласованию с управляющей организацией. Арматуру и привязки сверить по паспортам приборов.
8. Ст Т3-2 на обмере не показаны: приняты рядом с Ст В1-2 (в МКД стоят группой); положение сверить на объекте до разводки.
9. Штриховая линия чистовой грани стены прерывается на длине полотна открытой двери, лежащего вдоль грани (линии не должны сливаться при печати); положение грани — по размерам, а не по штриху.

					Проект: Четырёхкомнатная квартира
	Лист	№ док.	Подпись	Дата	Схема разводки водопровода и канализации
Дизайнер	Кырлан А.С.			04.11.26	

Стадия	Лист	Листов
П	23	120

Схема В1 (М 1:50; по вертикали и горизонтали один масштаб, глубина — ×0,5 под 45°)

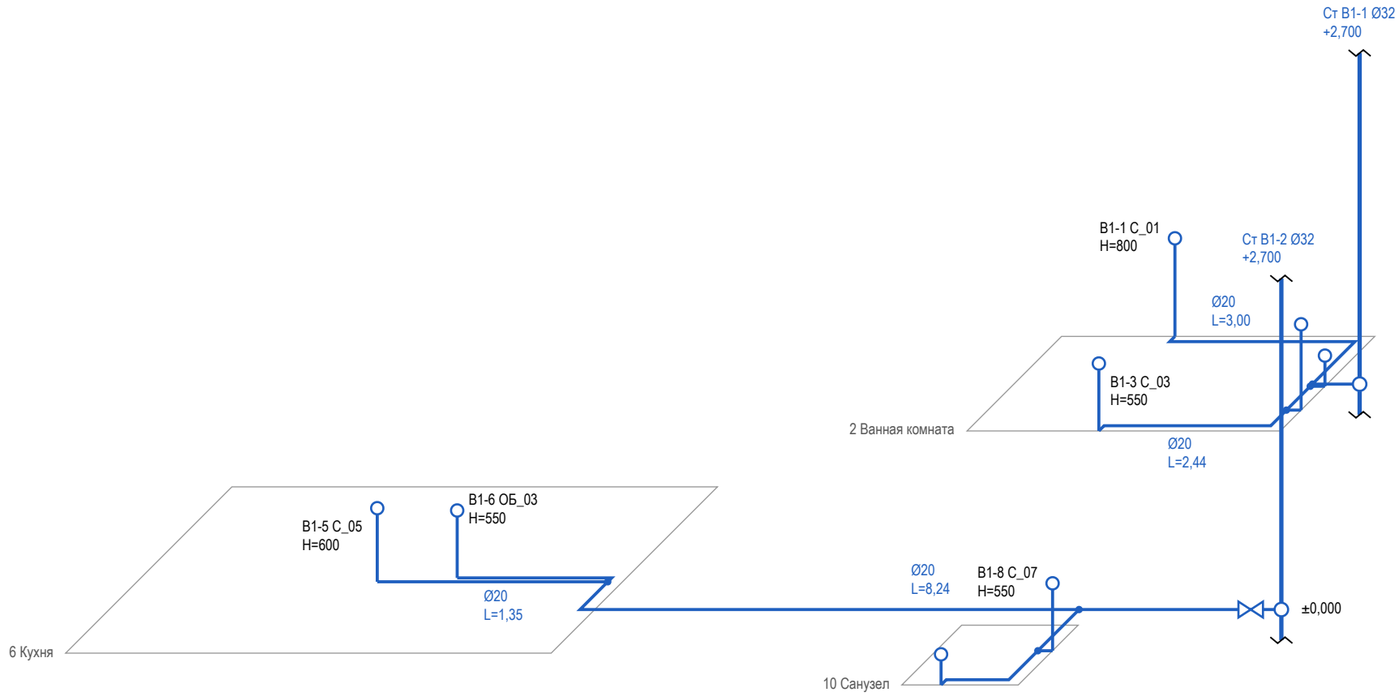

Условные обозначения


- В1 — водопровод хозяйственно-питьевой (ХВС), PP-R Ø20
- вывод В1 (код — в ведомости привязок)
- стояк «Ст К1-N / Ст В1-N» (ГОСТ 21.601), Ø мм
- стояк в плане (на отметке пола); вертикаль — стояк по высоте, разрыв — перекрытие
- тройник (ответвление к прибору)
- кран шаровой

Примечания

1. Схема В1 построена по тем же трассам, что план разводки: положение в плане сохранено, глубина — в масштабе ×0,5. Трассы принципиальные; фактическое положение фиксируется исполнительной схемой до закрытия.
2. Высоты H — от чистого пола помещения, мм. Отметка прокладки магистрали В1 (в стяжке, в стене или по полу) в данных не задана: участки показаны на уровне пола условно (записи реестра нет).
3. Узел ввода В1 (кран, фильтр, счётчик, обратный клапан, кран) — на схеме разводки; состав узла ввода — по согласованию. Кран шаровой — на первом участке от стояка.
4. Трубы испытать давлением до закрытия (акт скрытых работ, опрессовка по СП 73.13330.2016).
5. Диаметры, высоты выводов и места кранов — по паспортам выбранных приборов и расчёту проектной организации.
6. Расчёт систем, диаметры магистралей и подбор оборудования выполняет проектная организация.

					Проект: Четырёхкомнатная квартира	М 1:50
	Лист	№ док.	Подпись	Дата	Аксонометрическая схема В1 (холодное водоснабжение)	Стадия / Лист / Листов
Дизайнер	Кырлан А.С.			04.11.26		П / 24 / 120

Схема Т3 (М 1:50; по вертикали и горизонтали один масштаб, глубина — ×0,5 под 45°)

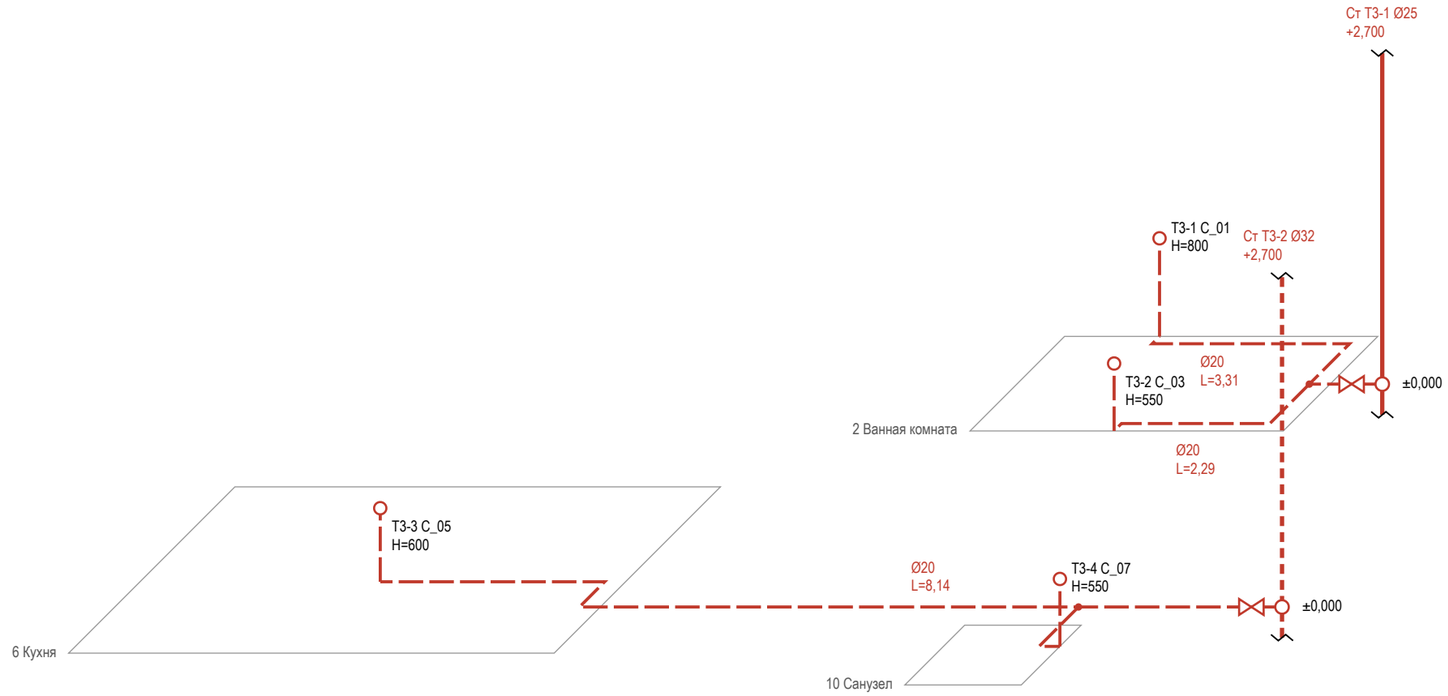

Условные обозначения


- Т3 — горячее водоснабжение, подача (ГВС), PP-R Ø20
- вывод Т3 (код — в ведомости привязок)
- стояк «Ст К1-N / Ст В1-N» (ГОСТ 21.601), Ø мм
- стояк в плане (на отметке пола); вертикаль — стояк по высоте, разрыв — перекрытие
- тройник (ответвление к прибору)
- кран шаровой
- стояк Т3 не на обмере — принят в шахте рядом со Ст В1, сверить

Примечания

1. Схема Т3 построена по тем же трассам, что план разводки: положение в плане сохранено, глубина — в масштабе ×0,5. Трассы принципиальные; фактическое положение фиксируется исполнительной схемой до закрытия.
2. Высоты Н — от чистого пола помещения, мм. Отметка прокладки магистрали Т3 (в стяжке, в стене или по полу) в данных не задана: участки показаны на уровне пола условно (записи реестра нет).
3. Узел ввода Т3 (кран, фильтр, счётчик, обратный клапан, кран) — на схеме разводки; состав узла ввода — по согласованию. Кран шаровой — на первом участке от стояка.
4. Циркуляция ГВС в данных не задана — циркуляционного трубопровода на схеме нет (записи реестра нет).
5. Ст Т3-2 на обмере не показаны: приняты рядом с Ст В1-2 (в МКД стоят группой); положение сверить на объекте до разводки.
6. Трубы испытать давлением до закрытия (акт скрытых работ, опрессовка по СП 73.13330.2016).
7. Диаметры, высоты выводов и места кранов — по паспортам выбранных приборов и расчёту проектной организации.
8. Расчёт систем, диаметры магистралей и подбор оборудования выполняет проектная организация.

					Проект: Четырёхкомнатная квартира		M 1:50
	Лист	№ док.	Подпись	Дата	Аксонометрическая схема Т3 (горячее водоснабжение)	Стадия	Лист	Листов
Дизайнер	Кырлан А.С.			04.11.26		П	25	120

Схема К1 (М 1:50; по вертикали и горизонтали один масштаб, глубина — ×0,5 под 45°)

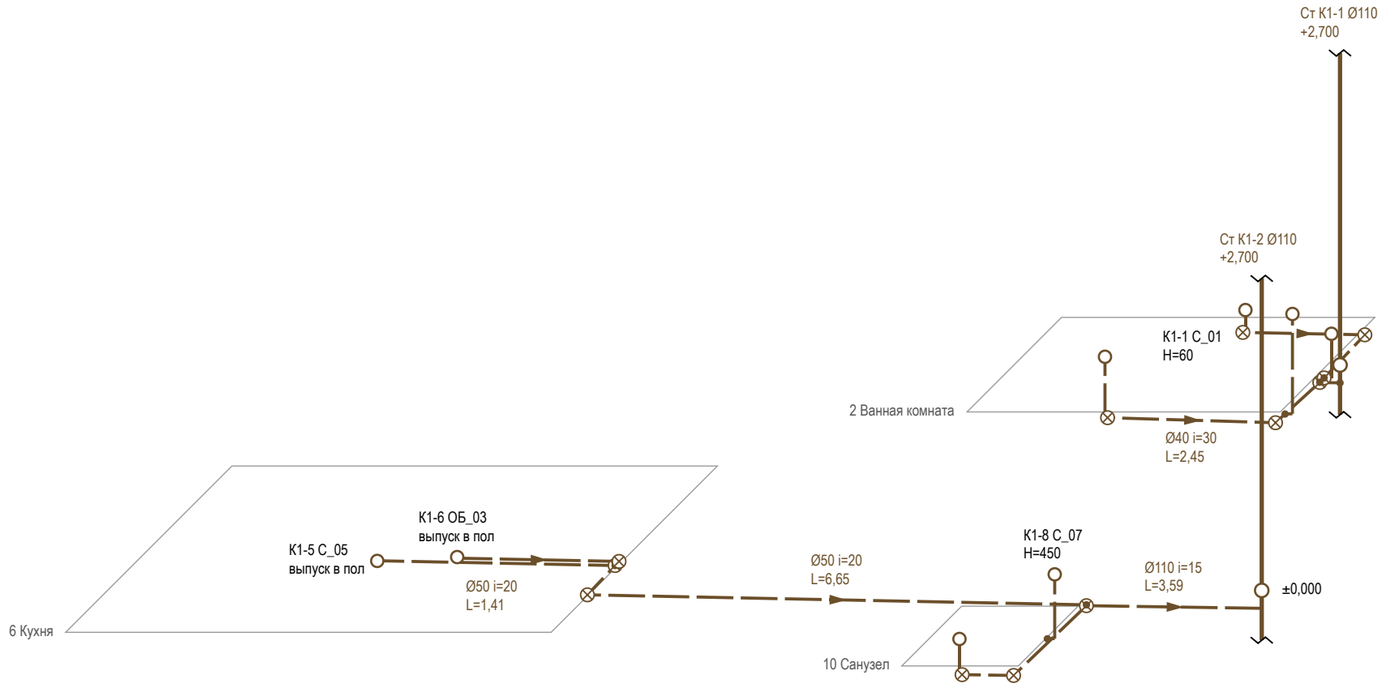

Условные обозначения


- К1 — канализация бытовая
- вывод К1 (код — в ведомости привязок)
- стояк «Ст К1-N / Ст В1-N» (ГОСТ 21.601), Ø мм
- стояк в плане (на отметке пола); вертикаль — стояк по высоте, разрыв — перекрытие
- направление уклона К1 / пола: Ø, мм на 1 м
- ревизия (прочистка) К1 — доступ сохранить
- тройник (ответвление к прибору)

Примечания


1. Схема К1 построена по тем же трассам, что план разводки: положение в плане сохранено, глубина — в масштабе ×0,5. Трассы принципиальные; фактическое положение фиксируется исполнительной схемой до закрытия.
2. Отметки — от плиты перекрытия: низ трубы у врезки в стояк — отметка из данных выпуска, к прибору труба поднимается на уклон i, мм/м (уклон не менее 1/d и не более 150 мм/м, СП 30.13330.2020, п. 19.1); чистый пол — выше плиты на стяжку (высота пирога пола). Высота выпуска прибора H — от чистого пола.
3. Ревизия — на повороте и в начале участка; стояк К1 в коробе с люком — звукоизоляция стояка в коробе; поворот — двумя отводами 45°.
4. Трубы испытать давлением до закрытия (акт скрытых работ, опрессовка по СП 73.13330.2016).
5. Диаметры, высоты выводов и места кранов — по паспортам выбранных приборов и расчёту проектной организации.
6. Расчёт систем, диаметры магистралей и подбор оборудования выполняет проектная организация.

					Проект: Четырёхкомнатная квартира		М 1:50
	Лист	№ док.	Подпись	Дата	Аксонометрическая схема К1 (канализация)	Стадия	Лист	Листов
Дизайнер	Кырлан А.С.			04.11.26		П	26	120

Стена А (М 1:20)

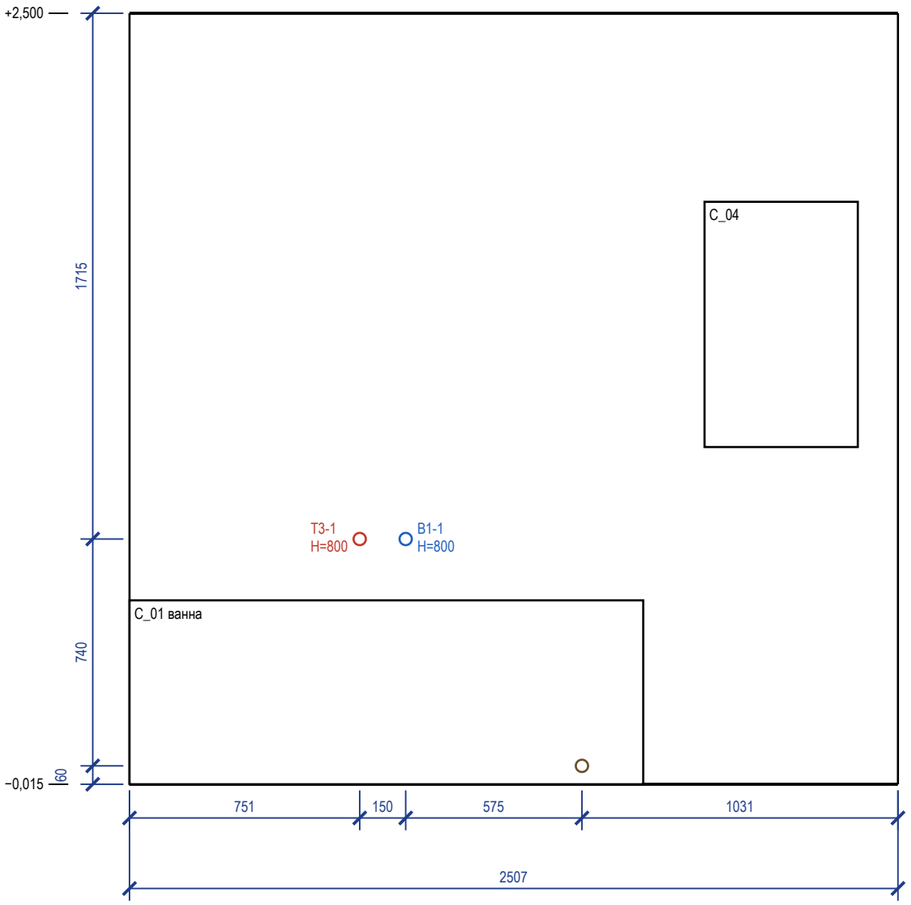

Стена Б (М 1:20)

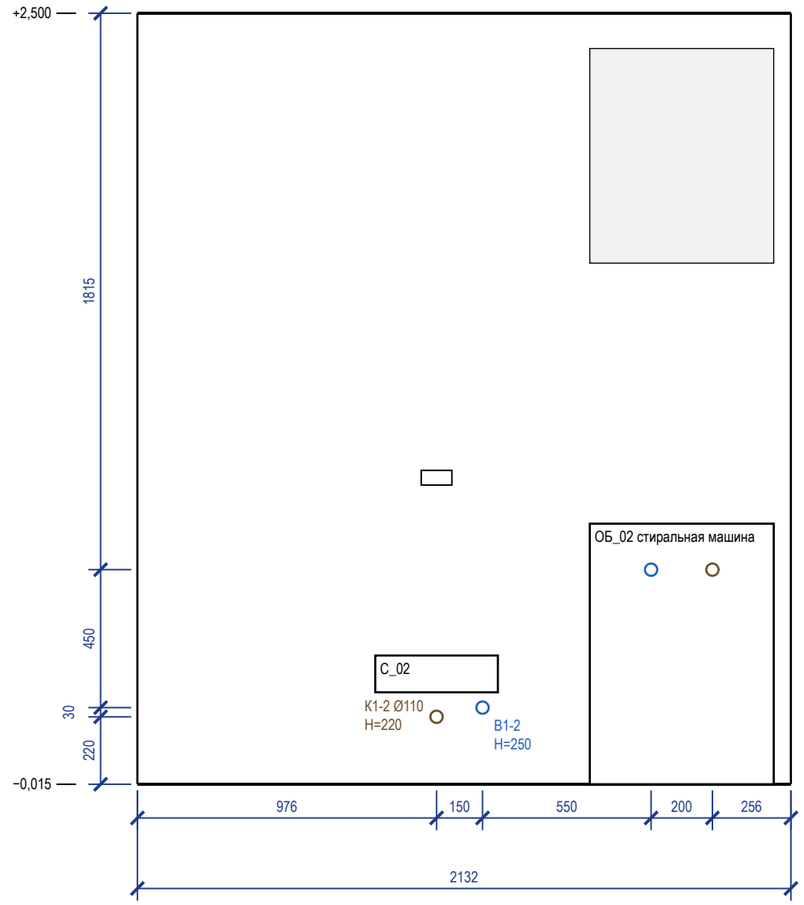

Ведомость привязок выводов (от чистого пола и угла)

Код	Прибор	Ø	H, мм	Привязка, мм
B1-1	C_01 ванна	½"	800	ст. А: 901 от лев. угла
T3-1	C_01 ванна	½"	800	ст. А: 751 от лев. угла
K1-1	C_01 ванна	Ø50	60	ст. А: 1476 от лев. угла
B1-2	C_02 унитаз подвесной	½"	250	ст. Б: 1126 от лев. угла
K1-2	C_02 унитаз подвесной	Ø110	220	ст. Б: 976 от лев. угла
B1-4	ОБ_02 стиральная машина	½"	700	ст. Б: 1676 от лев. угла
K1-4	ОБ_02 стиральная машина	Ø40	700	ст. Б: 1876 от лев. угла

Условные обозначения


- вывод B1 (код — в ведомости привязок)
- вывод T3 (код — в ведомости привязок)
- вывод K1 (код — в ведомости привязок)
- сантехприбор по расстановке (габарит модели)
- дверной проём; окно — сплошной контур
- кнопка смыва инсталляции (H — по данным прибора)

Примечания


1. Габариты и высоты приборов, межосевые смесителей и места кранов — по паспортам выбранных приборов, сверяются до разметки стен.
2. Высоты H — от чистого пола помещения, мм; отметка чистого пола и потолка — у левого края вида (от ±0,000 объекта). Привязки — от левого чистового угла вида (облицовка стен вычтена), как на развёртках стен.
3. Кнопка смыва C_02 — H=1000 (по данным прибора).
4. Ревизионные люки (ревизия K1 в коробе за стиральной машиной 300×400): место в стене на развёртке не задано (записи реестра нет).
5. Часть подписей выводов не уместилась у знака: коды и высоты — в ведомости привязок.
6. Помещение «Ванная комната» — 2 листа: стены 1) А, Б; 2) В, Г.
7. Расчёт систем водоснабжения и канализации и подбор оборудования выполняет проектная организация; лист задаёт места и высоты выводов.

					Проект: Четырёхкомнатная квартира	М 1:20
	Лист	№ док.	Подпись	Дата		
Дизайнер	Кырлан А.С.			04.11.26	Развёртки мокрых зон: выводы ВК. Ванная комната (лист 1 из 2)	Стадия: П; Лист: 27; Листов: 120

Стена В (М 1:20)

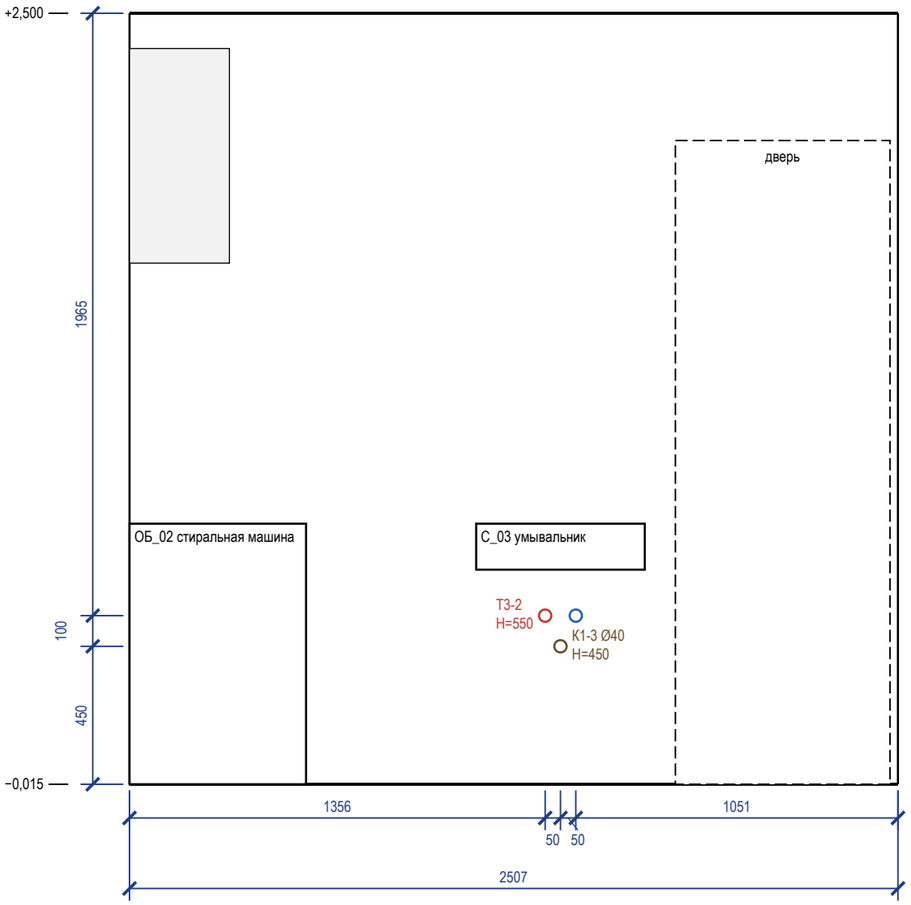

Стена Г (М 1:20)

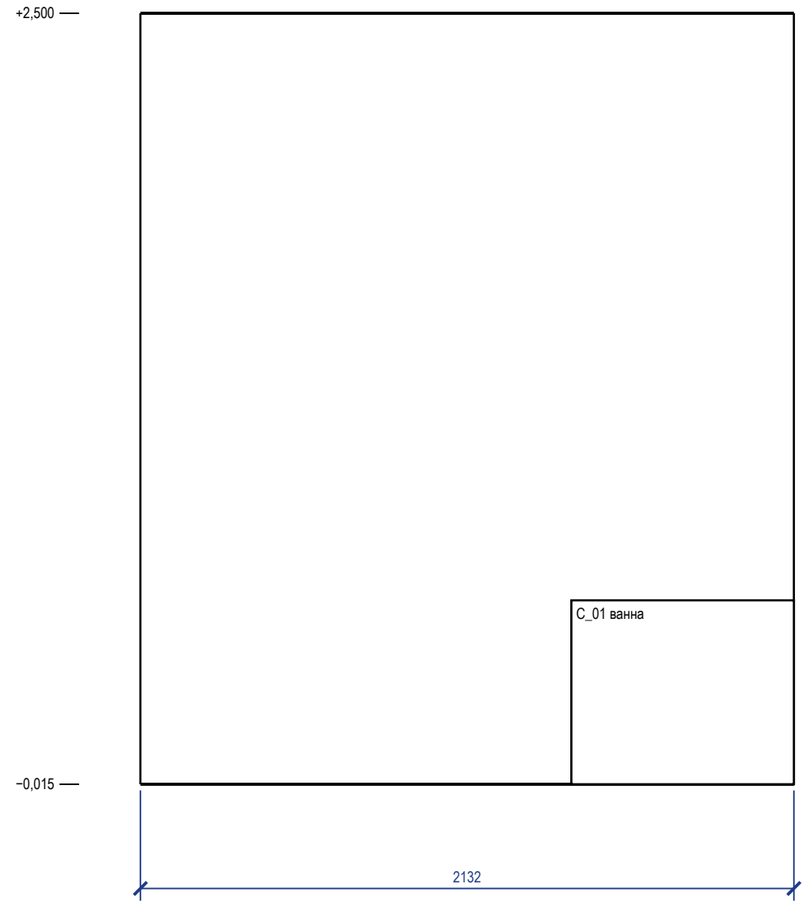

Ведомость привязок выводов (от чистого пола и угла)

Код	Прибор	Ø	H, мм	Привязка, мм
В1-3	С_03 умывальник	½"	550	ст. В: 1456 от лев. угла
Т3-2	С_03 умывальник	½"	550	ст. В: 1356 от лев. угла
К1-3	С_03 умывальник	Ø40	450	ст. В: 1406 от лев. угла

Условные обозначения

- вывод В1 (код — в ведомости привязок)
- вывод Т3 (код — в ведомости привязок)
- вывод К1 (код — в ведомости привязок)
- сантехприбор по расстановке (габарит модели)
- дверной проём; окно — сплошной контур

Примечания

1. Габариты и высоты приборов, межосевые смесителей и места кранов — по паспортам выбранных приборов, сверяются до разметки стен.
2. Высоты H — от чистого пола помещения, мм; отметка чистого пола и потолка — у левого края вида (от ±0,000 объекта). Привязки — от левого чистового угла вида (облицовка стен вычтена), как на развёртках стен.
3. Ревизионные люки (ревизия К1 в коробе за стиральной машиной 300×400): место в стене на развёртке не задано (записи реестра нет).
4. Часть подписей выводов не уместилась у знака: коды и высоты — в ведомости привязок.
5. Помещение «Ванная комната» — 2 листа: стены 1) А, Б; 2) В, Г.
6. Расчёт систем водоснабжения и канализации и подбор оборудования выполняет проектная организация; лист задаёт места и высоты выводов.

					Проект: Четырёхкомнатная квартира — М 1:20
	Лист	№ док.	Подпись	Дата	
Дизайнер	Кырлан А.С.			04.11.26	Развёртки мокрых зон: выводы ВК. Ванная комната (лист 2 из 2)

Стадия	Лист	Листов
П	28	120

Ведомость привязок выводов (от чистого пола и угла)

Код	Прибор	Ø	H, мм	Привязка, мм
Стен с приборами нет. Развёртка не построена: выводы В1, Т3, К1 не назначены, привязки не даются; расстановка приборов в данных не задана (записи реестра нет).				
	выводов на стене нет			

Условные обозначения


- вывод В1 (код — в ведомости привязок)
- вывод Т3 (код — в ведомости привязок)
- вывод К1 (код — в ведомости привязок)
- сантехприбор по расстановке (габарит модели)
- дверной проём; окно — сплошной контур

Примечания


1. Габариты и высоты приборов, межосевые смесителей и места кранов — по паспортам выбранных приборов, сверяются до разметки стен.
2. Высоты H — от чистого пола помещения, мм; отметка чистого пола и потолка — у левого края вида (от ±0,000 объекта). Привязки — от левого чистового угла вида (облицовка стен вычтена), как на развёртках стен.
3. Приборы С_05, ОБ_03: стена не определена, на развёртке не показаны (записи реестра нет).
4. Выводы в полу (К1-1, К1-2): трап, лоток, выпуск отдельностоящей ванны, подвод к стойке напольного смесителя — на развёртке их нет; место и пирог пола — лист «Схема разводки» (профиль К1, узел 1).
5. Ревизионные люки к арматуре и ревизиям в данных не заданы: место и размер не определены (записи реестра нет).
6. Мойка, ПММ и фильтр — выводы в шкафу мойки; диаметры и положение сифона и кранов сверить по паспортам приборов и чертежам модуля.
7. Расчёт систем водоснабжения и канализации и подбор оборудования выполняет проектная организация; лист задаёт места и высоты выводов.

					Проект: Четырёхкомнатная квартира	**М 1:20**
	Лист	№ док.	Подпись	Дата		
Дизайнер	Кырлан А.С.			04.11.26	Развёртки мокрых зон: выводы ВК. Кухня	Стадия: П; Лист: 29; Листов: 120

Стена Б (М 1:20)

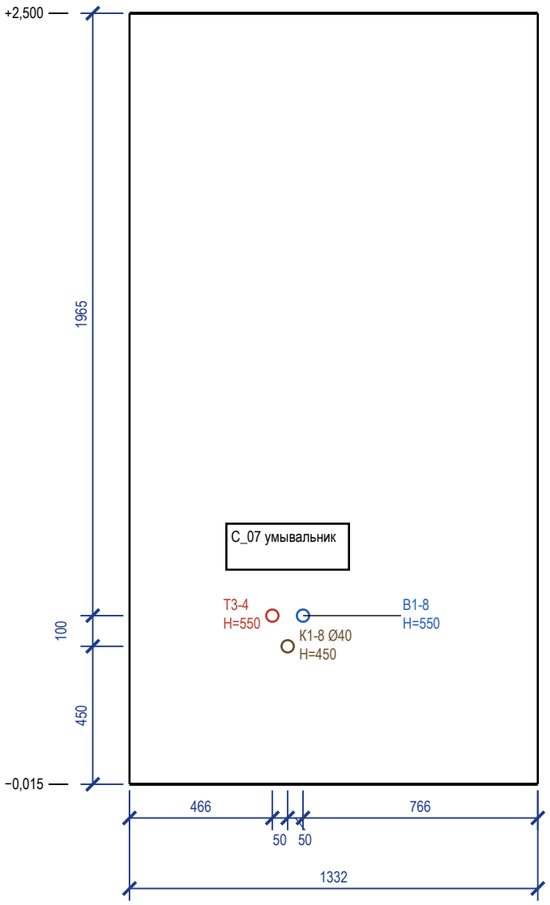

Стена В (М 1:20)

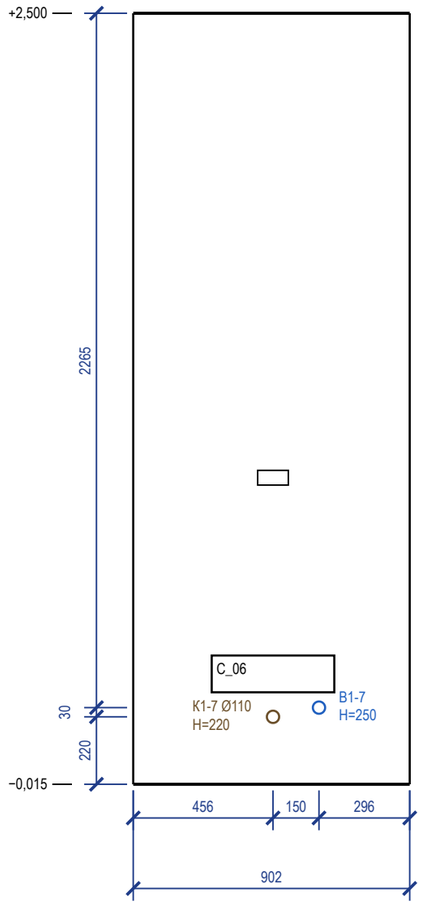

Ведомость привязок выводов (от чистого пола и угла)

Код	Прибор	Ø	H, мм	Привязка, мм
B1-8	C_07 умывальник	½"	550	ст. Б: 566 от лев. угла
T3-4	C_07 умывальник	½"	550	ст. Б: 466 от лев. угла
K1-8	C_07 умывальник	Ø40	450	ст. Б: 516 от лев. угла
B1-7	C_06 унитаз подвесной	½"	250	ст. В: 606 от лев. угла
K1-7	C_06 унитаз подвесной	Ø110	220	ст. В: 456 от лев. угла

Условные обозначения

- вывод B1 (код — в ведомости привязок)
- вывод T3 (код — в ведомости привязок)
- вывод K1 (код — в ведомости привязок)
- сантехприбор по расстановке (габарит модели)
- дверной проём; окно — сплошной контур
- кнопка смыва инсталляции (H — по данным прибора)

Примечания

1. Габариты и высоты приборов, межосевые смесителей и места кранов — по паспортам выбранных приборов, сверяются до разметки стен.
2. Высоты H — от чистого пола помещения, мм; отметка чистого пола и потолка — у левого края вида (от ±0,000 объекта). Привязки — от левого чистового угла вида (облицовка стен вычтена), как на развёртках стен.
3. Кнопка смыва C_06 — H=1000 (по данным прибора).
4. Ревизионные люки к арматуре и ревизиям в данных не заданы: место и размер не определены (записи реестра нет).
5. Расчёт систем водоснабжения и канализации и подбор оборудования выполняет проектная организация; лист задаёт места и высоты выводов.

					Проект: Четырёхкомнатная квартира	М 1:20
	Лист	№ док.	Подпись	Дата		
Дизайнер	Кырлан А.С.			04.11.26	Развёртки мокрых зон: выводы ВК. Санузел	Стадия: П; Лист: 30; Листов: 120


Поз.	Наименование и техническая характеристика	Тип, марка, обозначение документа	Код продукции	Поставщик	Ед. изм.	Кол.	Масса 1 ед., кг	Примечание
	Санитарные приборы							
1	Ванна встраиваемая акриловая 1700×750 мм, с каркасом, экраном и отверстием слив-перелив	аналог		выбор заказчика	шт	1	35	С_01
2	Унитаз подвесной безободковый, с сиденьем микролифт, крепёж и звукоизолирующая прокладка	аналог		выбор заказчика	шт	2		С_02, С_06
3	Инсталляция для подвесного унитаза: рама высотой 1120 мм, бачок, клавиша смыва (ось клавиши 1050 мм от чистого пола)	аналог		выбор заказчика	шт	2		С_02, С_06; короб ГКЛВ
4	Умывальник подвесной 550×450 мм, с отверстием под смеситель и переливом	аналог		выбор заказчика	шт	1		С_03
5	Умывальник подвесной 400×200 мм, с отверстием под смеситель и переливом	аналог		выбор заказчика	шт	1		С_07
6	Мойка кухонная врезная 760×480 мм, с переливом	аналог		с кухонной мебелью	шт	1		С_05
7	Полотенцесушитель электрический, IP44, с терморегулятором	аналог		выбор заказчика	шт	1		С_04
	Смесители, сифоны и арматура приборов							
8	Смеситель для ванны настенный однорычажный, межосевое 150 мм, с душевым набором (лейка, шланг, держатель)	аналог		выбор заказчика	шт	1		С_01
9	Смеситель для умывальника однорычажный, с донным клапаном	аналог		выбор заказчика	шт	2		С_03, С_07
10	Смеситель кухонный однорычажный, высокий излив	аналог		выбор заказчика	шт	1		С_05
11	Обвязка ванны слив-перелив Ø40/50 с сифоном	аналог		выбор заказчика	шт	1		С_01
12	Сифон для умывальника бутылочный Ø32/40–50, с гофрой к выпуску	аналог		выбор заказчика	шт	2		С_03, С_07
13	Сифон для мойки Ø40/50	аналог		выбор заказчика	шт	1		С_05
14	Сифон для посудомоечной машины с обратным клапаном, на выводе слива Ø40	аналог		выбор заказчика	шт	1		ОБ_03
15	Сифон для стиральной машины встраиваемый в стену Ø50, с обратным клапаном	аналог		выбор заказчика	шт	1		ОБ_02
16	Кран угловой ½"×½" с гибкой подводкой 40 см (умывальники, мойка)	аналог		выбор заказчика	шт	6		по 2 на прибор
17	Кран шаровой угловой ½"×¾" для подключения стиральной и посудомоечной машины	аналог		выбор заказчика	шт	2		ОБ_02, ОБ_03
	Трубопроводы							
18	Труба полипропиленовая PP-R PN20 Ø20×3,4 (В1)	ГОСТ 32415-2013		выбор заказчика	м	24,5	0,17	17,6 + 4,3 + 10 %
19	Труба PP-R, армированная стекловолокном, PN20 Ø20×2,8 (Т3)	ГОСТ 32415-2013		выбор заказчика	м	19,5	0,15	14,8 + 2,5 + 10 %
20	Труба канализационная ПП Ø40 (К1)	ГОСТ 32414-2013		выбор заказчика	м	5		2,6 + 1,6 + 10 %
21	Труба канализационная ПП Ø50 (К1)	ГОСТ 32414-2013		выбор заказчика	м	12,5		10,1 + 1,0 + 10 %
22	Труба канализационная ПП Ø110 (К1)	ГОСТ 32414-2013		выбор заказчика	м	5		3,9 + 0,4 + 10 %
	Фасонные части и выводы							
23	Отвод канализационный ПП 45° Ø40	ГОСТ 32414-2013		выбор заказчика	шт	4		2 шт. на поворот
24	Отвод канализационный ПП 45° Ø50	ГОСТ 32414-2013		выбор заказчика	шт	10		2 шт. на поворот
25	Отвод канализационный ПП 45° Ø110	ГОСТ 32414-2013		выбор заказчика	шт	10		2 шт. на поворот
26	Тройник канализационный ПП 45° (врезки ветвей)	ГОСТ 32414-2013		выбор заказчика	шт	7		
27	Ревизия канализационная ПП (после поворота трассы)	ГОСТ 32414-2013		выбор заказчика	шт	6		доступ сохранить
28	Фитинги PP-R Ø20: тройники, угольники 90° (ветви и повороты В1, Т3)	ГОСТ 32415-2013		выбор заказчика	шт	28		
29	Водорозетка PP-R Ø20×½" настенная, с креплением	ГОСТ 32415-2013		выбор заказчика	шт	12		коды — лист выводов
	Узлы ввода, люки, короба							
30	Кран шаровой латунный Ду15 PN16 (отключение ввода)	аналог		выбор заказчика	шт	4		Ст В1-1, Ст Т3-1, Ст В1-2, Ст Т3-2
31	Фильтр сетчатый косой Ду15	аналог		выбор заказчика	шт	4		
32	Счётчик воды крыльчатый Ду15 (ХВ, ГВ), с поверкой	аналог		выбор заказчика	шт	4		пломба УК
33	Клапан обратный Ду15	аналог		выбор заказчика	шт	4		
34	Люк ревизионный нажимной под плитку 300×400 мм	аналог		выбор заказчика	шт	4		к стоякам и арматуре
35	Звукоизоляция стояка К1 в коробе: рулонный звукоизоляционный материал ≥ 10 мм, обмотка стояка на высоту этажа	аналог		выбор заказчика	м	5,4		Ст К1-1, Ст К1-2
36	Короб К1 над полом: профиль ПН/ПС, ГКЛВ 12,5 мм под плитку	аналог		выбор заказчика	м	5,8		сечение — лист разводки

Примечания

1. Форма 1 ГОСТ 21.110-2013, ширины граф изменены по п. 4.1. «Аналог» — аналог по характеристикам: модели внести до черновых работ, привязки выводов сверить по паспортам.
2. Бытовая техника не входит (показана арматура подключения), мойка — в комплекте кухни (марка — модуля кухни, как у столяра). Длины труб — трасса листа разводки + подъёмы + 10 %.
3. Стояк К1 в коробе — звукоизоляция стояка в коробе без жёсткого контакта короба с трубой.
4. Расчёт систем водоснабжения и канализации, диаметры магистралей и подбор оборудования выполняет проектная организация.

					Проект: Четырёхкомнатная квартира
	Лист	№ док.	Подпись	Дата	Спецификация сантехнического оборудования
Дизайнер	Кырлан А.С.			04.11.26	

Стадия	Лист	Листов
П	31	120

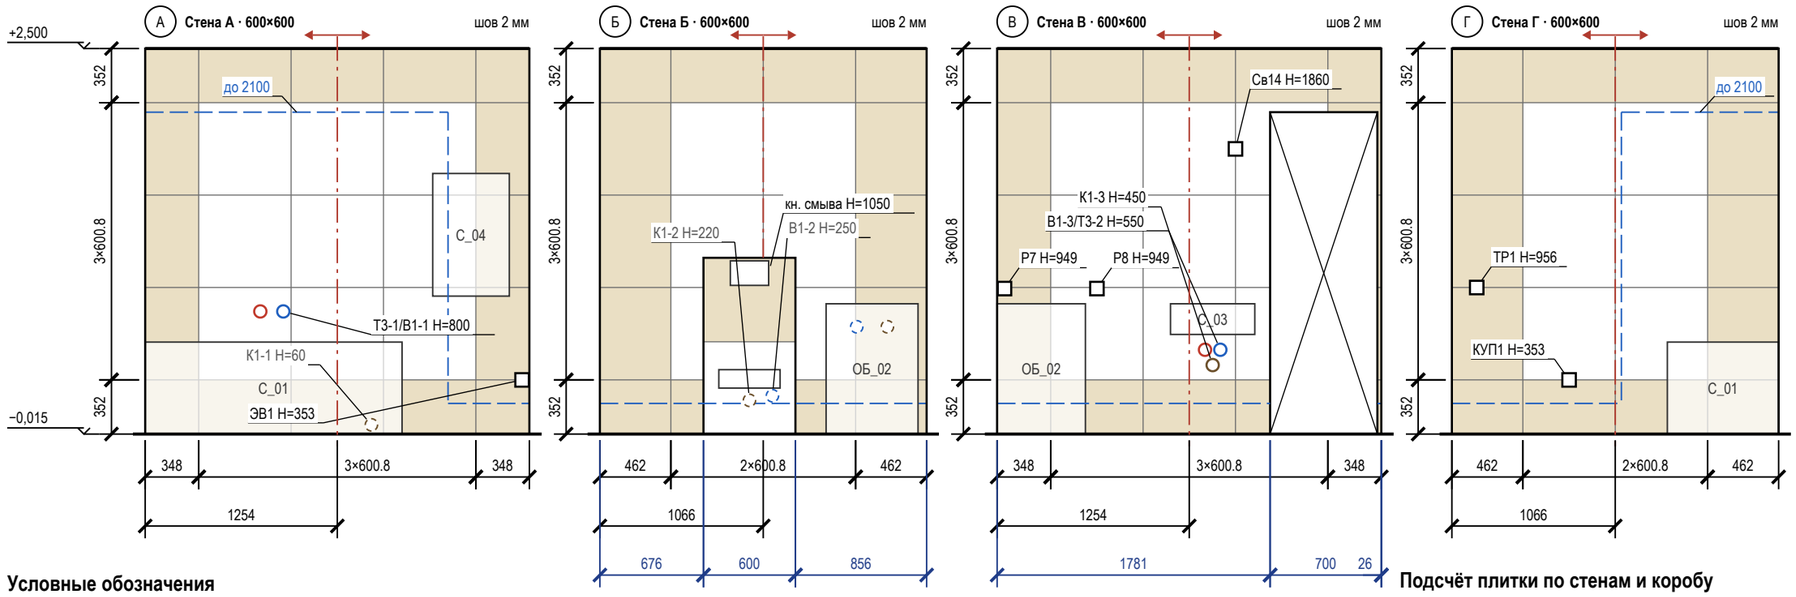

Условные обозначения

- плитка целая; тонкая линия — шов
- плитка с подрезкой (размер — на цепочке)
- ось старта; стрелки — направление укладки
- верх гидроизоляции: 200 от ЧП, в мокрой зоне — «до …»
- проём — не облицовывается
- сантехприбор: габарит, высота по практике
- короб инсталляции, в нём кнопка смыва 250×160
- вывод В1 (код — в ведомости привязок)
- вывод Т3 (код — в ведомости привязок)
- вывод К1 (код — в ведомости привязок)
- вывод за прибором / в коробе (не на сетке)
- электроточка: марка и Н — по листам ЭОМ
- отметка уровня, м: ±0,000 — чистый пол жилых помещений
- низ потолка; серая полоса — стена без плитки
- (А) обозначение стены А–Г (как на развёртках)

Примечания

1. Вид изнутри, стены по часовой стрелке А → Г. Высоты — от чистого пола (−0,015), отметки — от ±0,000. Раскладка от чистовых размеров (штукатурка 10 + клей 5 + плитка 9 мм), подрезки чистые; старт — от оси стены, ряды от середины (две подрезки).
2. Облицовка до потолка (+2,500).
3. Открытые выводы и электроточки — на шве или в центре плитки (допуск 10 мм; плитка от 900 мм по высоте — на шве или не ближе 60 мм к нему).
4. Выводы ВК стоят по оси прибора и с прибором не двигаются — привязки по «Плану выводов сантехники» без сдвига; вне сетки (Т3-1/В1-1, В1-3/Т3-2, К1-3) отверстие в плитке коронкой по той же привязке, плитку не сдвигать.
5. За приборами и в коробе (К1-1, В1-2, К1-2, В1-4, К1-4) — штриховым кольцом.
6. Гидроизоляция: 200 мм от ЧП по периметру; над ванной — до 2100 и 300 мм за борт (СП 29.13330.2011, п. 7.2 — на высоту замачивания); углы — лентой; акт скрытых работ, пролив.
7. Короб 600×1150×230: лицо 600 мм от оси кнопки смыва, боковины, полка; углы — запил 45° или профиль; за коробом плитку не кладут.
8. Наружные углы: ст. Б: 2 — запил 45°; ст. В: 2 — профиль.
9. Люки: Л1 (ст. Б, 600×600, нажимной) — кромки дверцы по швам сетки.


Подсчёт плитки по стенам и коробу

Поверхность	L × H, мм	S, м²	Целых	Подр.	С запасом	Подрезки: край / верх, мм
стена А	2507 × 2515	6,43	9	16	28	348 / 348; 352
стена Б	2132 × 2515	4,79	2	18	22	462 / 462; 352
короб (ст. Б)	600×1150×230	1,36	1	6	8	лицо 600; бок. 230
стена В	2507 × 2515	4,96	6	19	28	348 / 348; 352
стена Г	2132 × 2515	5,48	6	14	22	462 / 462; 352
Итого		**23,01**	**24**	**73**	**108**	

					Проект: Четырёхкомнатная квартира — **М 1:40**
	Лист	№ док.	Подпись	Дата	Раскладка плитки. Ванная комната. Развёртки стен
Дизайнер	Кырлан А.С.			04.11.26	

Стадия	Лист	Листов
П	32	120

выпуск 04.11.2026 № 2391fcbada · стр. 32 из 120

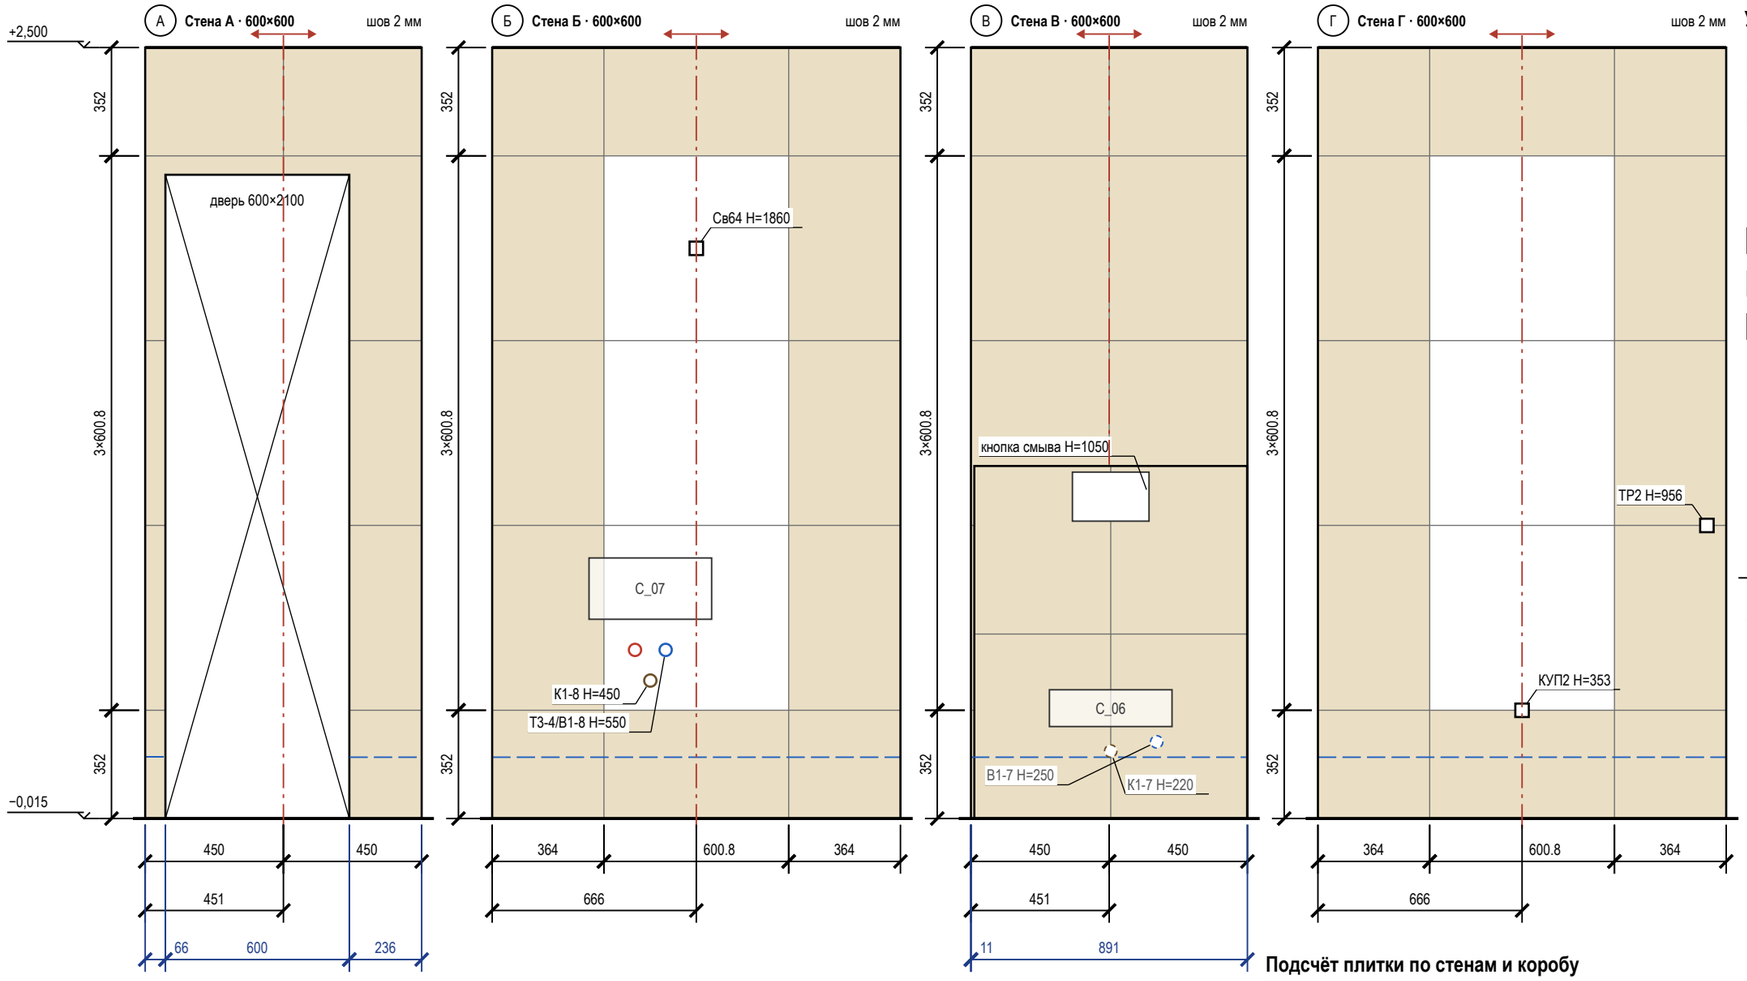

Условные обозначения

- плитка целая; тонкая линия — шов
- плитка с подрезкой (размер — на цепочке)
- ось старта; стрелки — направление укладки
- верх гидроизоляции: 200 от ЧП, в мокрой зоне — «до …»
- проём — не облицовывается
- сантехприбор: габарит, высота по практике
- короб инсталляции, в нём кнопка смыва 250×160
- вывод В1 (код — в ведомости привязок)
- вывод Т3 (код — в ведомости привязок)
- вывод К1 (код — в ведомости привязок)
- вывод за прибором / в коробе (не на сетке)
- электроточка: марка и Н — по листам ЭОМ
- отметка уровня, м: ±0,000 — чистый пол жилых помещений
- низ потолка; серая полоса — стена без плитки
- (А) обозначение стены А–Г (как на развёртках)

Примечания


1. Вид изнутри, стены по часовой стрелке А → Г. Высоты — от чистого пола (−0,015), отметки — от ±0,000. Раскладка от чистовых размеров (штукатурка 10 + клей 5 + плитка 9 мм), подрезки чистые; старт — от оси стены, ряды от середины (две подрезки).
2. Облицовка до потолка (+2,500).
3. Открытые выводы и электроточки — на шве или в центре плитки (допуск 10 мм; плитка от 900 мм по высоте — на шве или не ближе 60 мм к нему).
4. Выводы ВК стоят по оси прибора и с прибором не двигаются — привязки по «Плану выводов сантехники» без сдвига; вне сетки (Т3-4/В1-8, К1-8) — отверстие в плитке коронкой по той же привязке, плитку не сдвигать.
5. За приборами и в коробе (В1-7, К1-7) — штриховым кольцом.
6. Гидроизоляция: 200 мм от ЧП по периметру; углы — лентой; акт скрытых работ, пролив.
7. Короб 890×1150×230: лицо 444 / 444 мм от оси кнопки смыва, боковины, полка; углы — запил 45° или профиль; за коробом плитку не кладут.
8. Между коробом и углом полоса 11 мм — довести короб до угла.
9. Наружные углы: ст. А: 2 — профиль.

Подсчёт плитки по стенам и коробу

Поверхность	L × H, мм	S, м²	Целых	Подр.	С запасом	Подрезки: край / верх, мм
стена А	902 × 2515	1,13	0	10	11	450 / 450; 352
стена Б	1332 × 2515	3,47	3	12	17	364 / 364; 352
стена В	902 × 2515	1,37	0	10	11	450 / 450; 352
короб (ст. В)	890×1150×230	1,76	0	10	11	лицо 444 / 444; бок. 230
стена Г	1332 × 2515	3,47	3	12	17	364 / 364; 352
Итого		**11,19**	**6**	**54**	**67**	

	Лист	№ док.	Подпись	Дата	Проект: Четырёхкомнатная квартира — **М 1:20**
Дизайнер	Кырлан А.С.			04.11.26	Раскладка плитки. Санузел. Развёртки стен

Стадия	Лист	Листов
П	33	120

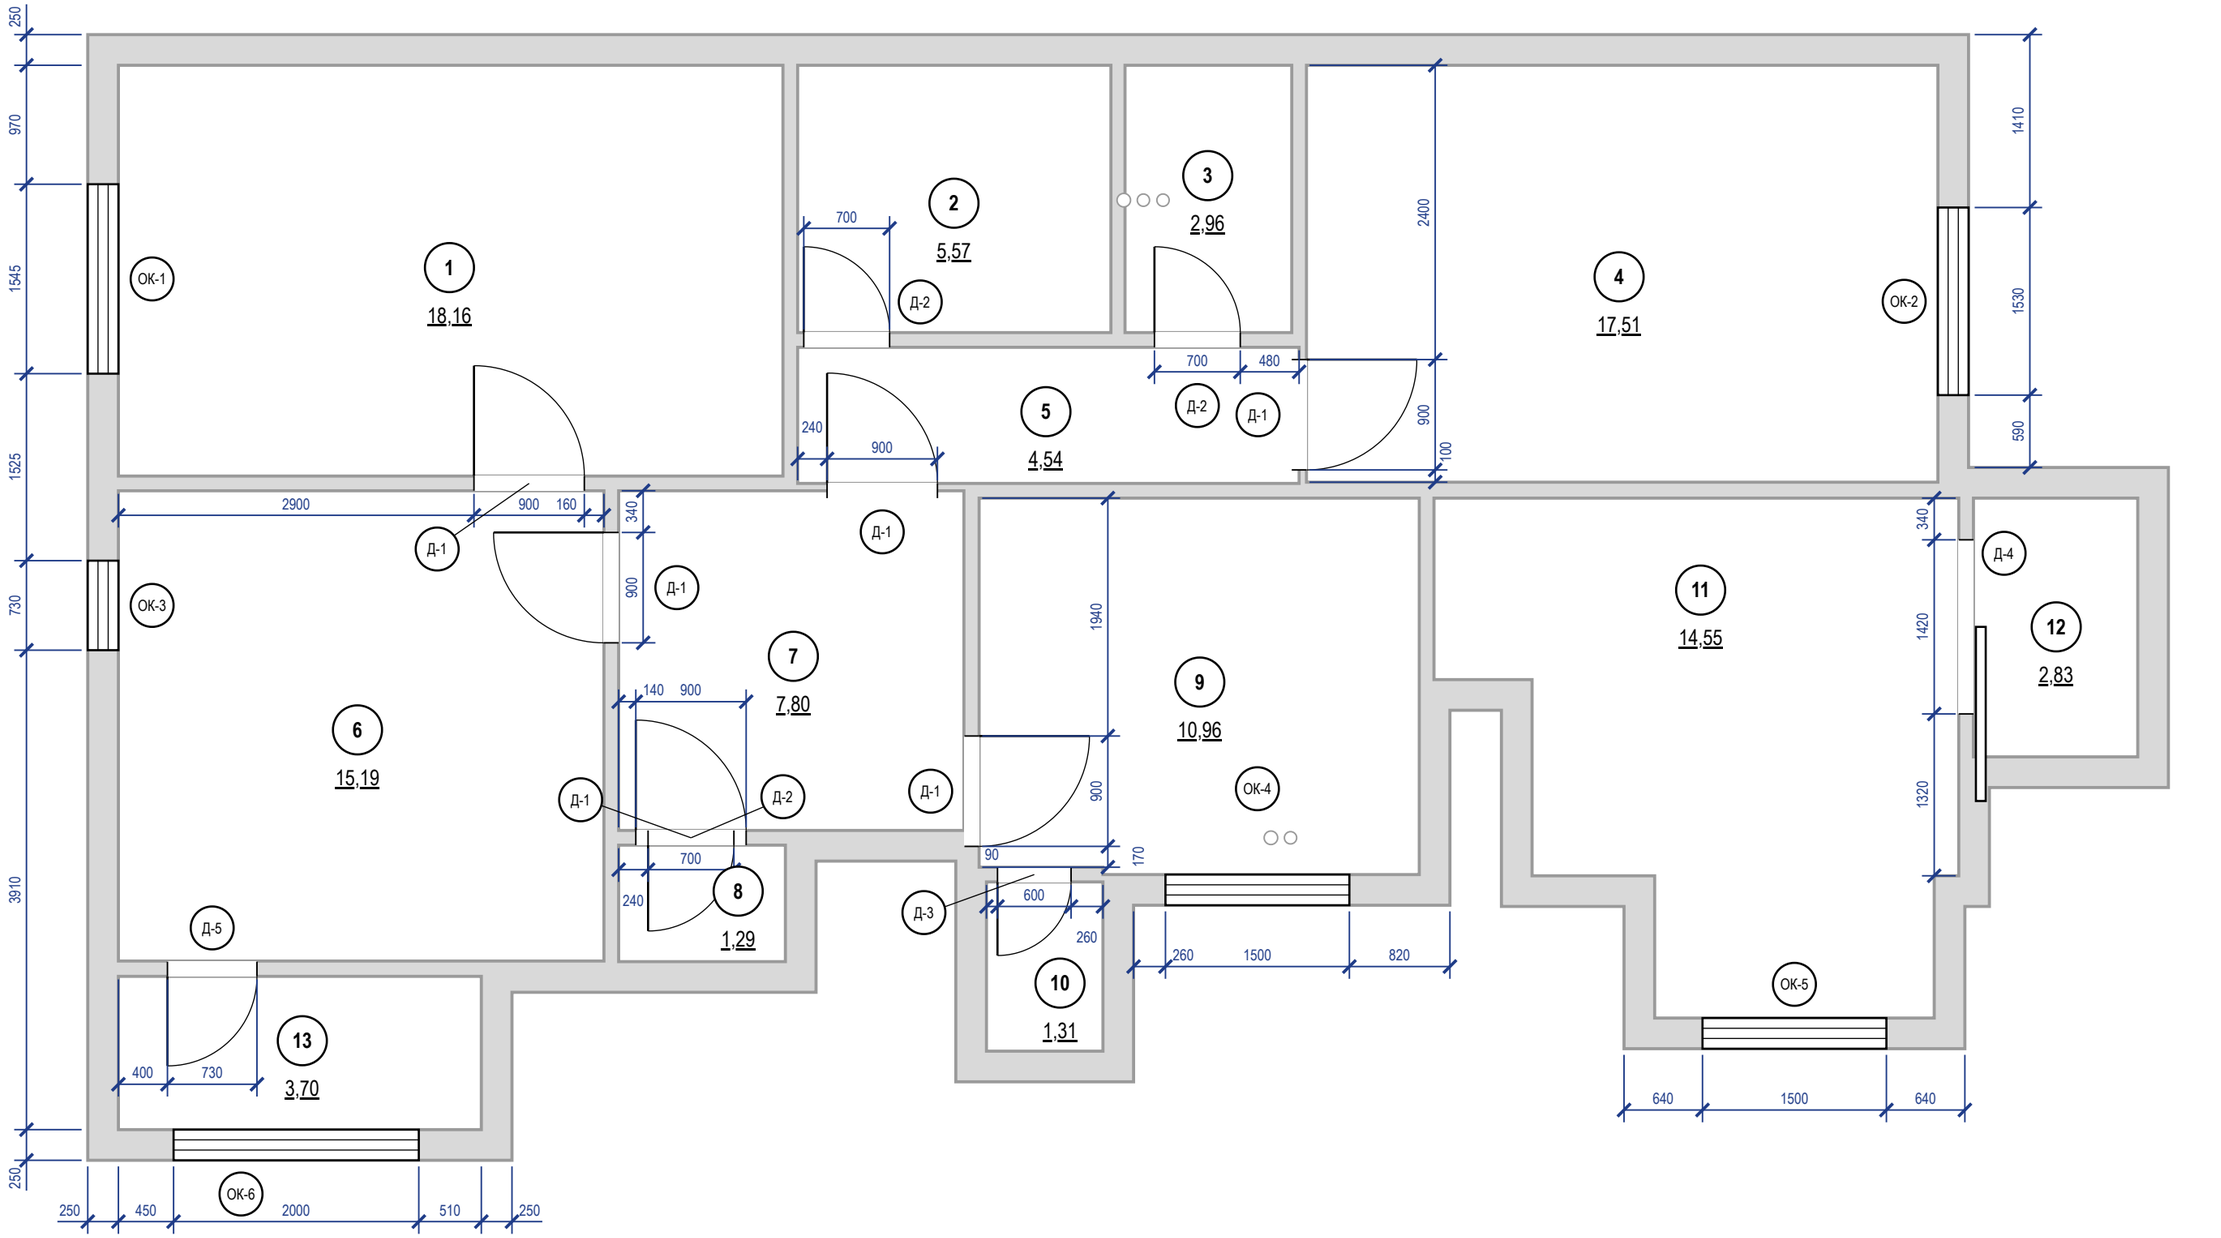

Примечания


1. Размеры проёмов и привязки — в миллиметрах от чистых граней стен до отделки; привязка — от угла того помещения, со стороны которого стоит размер. Размер проёма — ширина × высота от чистого пола 0,000. Размеры на плане — проёмов, не полотен: полотно — в ведомости, коробка — по системе.
2. Марки в кружках — типы заполнения проёмов (ГОСТ 21.501-2018, п. 5.3.2); одна марка — один типоразмер; количество сверено с планом.
3. Размеры проёмов и привязки сняты со скана плана заказчика и на объекте не замерены (обмерный план — лист 6).
4. Экспликация помещений — лист 6; в марках помещений — номер и площадь, м².
5. Ведомость заполнения проёмов, открывание полотен, заказ и порядок монтажа блоков — лист 35.
6. Привязка проёма к углу помещения меньше 1 мм на листе, размер на плане не показан: Д-2 — 50 мм.

					Проект: Четырёхкомнатная квартира	М 1:50
	Лист	№ док.	Подпись	Дата		
Дизайнер	Кырлан А.С.			04.11.26	План размещения дверей	Стадия / Лист / Листов
						П / 34 / 120

Ведомость заполнения проёмов

Марка	Наименование, обозначение	Проём ш×в, мм	Полотно (расч.)	Кол.	Откр.	Отделка полотна	Фурнитура	Прим.
Д-1	Блок дверной внутренний, ГОСТ 475-2016	900×2100	800×2000	6	П, П, П, Л, П, П		петли, ручка с защёлкой	пом. 5; б/п
Д-2	Блок дверной внутренний, ГОСТ 475-2016	700×2100	600×2000	3	П, П, Л		петли, ручка с защёлкой, фиксатор WC	пом. 2; порог 15
Д-3	Блок дверной внутренний, ГОСТ 475-2016	600×2100	не задано (записи реестра нет)	1	Л		петли, ручка с защёлкой, фиксатор WC	порог 15
Д-4	Дверь раздвижная, ГОСТ 475-2016	1420×2100	не задано (записи реестра нет)	1			раздвижная система, ручки-купе	пом. 12; б/п
Д-5	Блок дверной внутренний, ГОСТ 475-2016	730×2100	не задано (записи реестра нет)	1	Л		петли, ручка с защёлкой	порог 30
ОК-1	Блок оконный, ГОСТ 23166-2021	1545×1600		1				низ 800
ОК-2	Блок оконный, ГОСТ 23166-2021	1530×1600		1				низ 800
ОК-3	Блок оконный, ГОСТ 23166-2021	730×1600		1				низ 800
ОК-4	Блок оконный, ГОСТ 23166-2021	1500×1600		1				пом. 9; низ 800
ОК-5	Блок оконный, ГОСТ 23166-2021	1500×1600		1				пом. 11; низ 900
ОК-6	Блок оконный, ГОСТ 23166-2021	2000×1700		1				низ 900


Схемы дверных блоков (1:25) — вид со стороны открывания; вершина треугольника — сторона петель

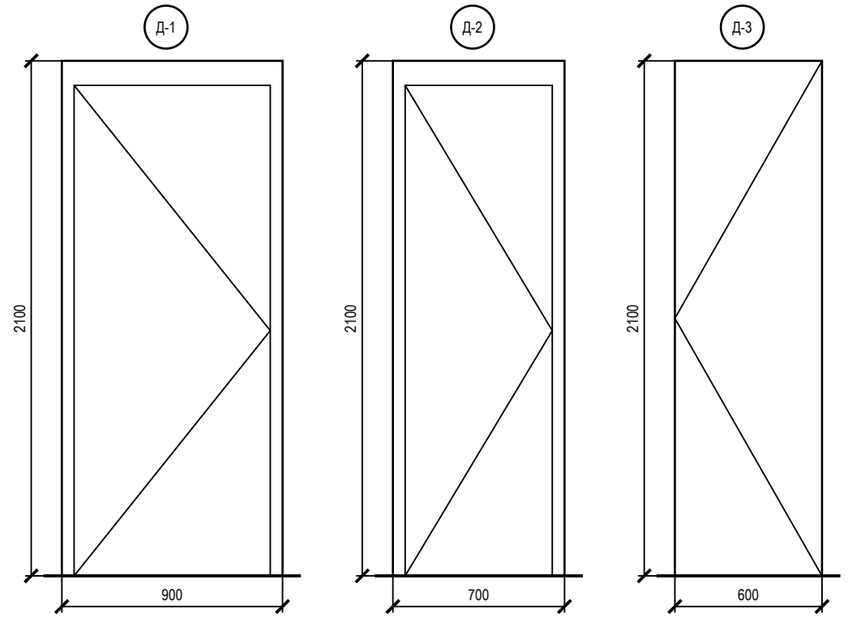

полотно 800×2000 (расч.)
откр. П, П, П, Л, П, П (схема — П, остальные по плану)

полотно 600×2000 (расч.)
откр. П, П, Л (схема — П, остальные по плану)

полотно не задано (записи реестра нет)
откр. Л

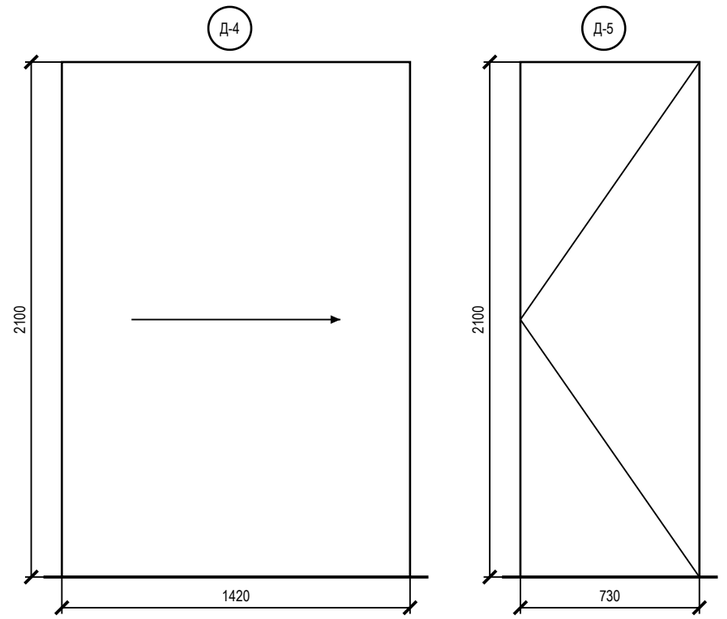

полотно не задано (записи реестра нет)
раздвижная


полотно не задано (записи реестра нет)
откр. Л

Примечания

1. Марки проёмов — те же, что на плане размещения дверей (лист 34); привязки проёмов — там же.
2. Открывание: Л — петли слева, П — справа, если смотреть со стороны, куда открывается полотно (на себя).
3. Дверные блоки обычного монтажа (Д-1…Д-5) заказывать после чистовой стяжки и штукатурки, проёмы перемерить; монтажный зазор коробки 10–15 мм на сторону, откос от угла помещения до коробки — не менее 50 мм.
4. Полотно «расч.» — по проёму с запасом по каталогам, заказ — по таблице проёмов модели; Д-1, Д-2: проём 2100, а под полотно 2000 по каталогам нужен 2040–2080, под 2100 2140–2180: высоту проёма — по модели; Д-3: проём 600×2100 вне ряда стандартных полотен — полотно задать при выборе модели; Д-4: раздвижная, полотно — по системе — полотно задать при выборе модели; Д-5: проём 730×2100 вне ряда стандартных полотен — полотно задать при выборе модели.

					Проект: Четырёхкомнатная квартира
	Лист	№ док.	Подпись	Дата	
Дизайнер	Кырлан А.С.			04.11.26	Ведомость заполнения проёмов

Стадия	Лист	Листов
П	35	120

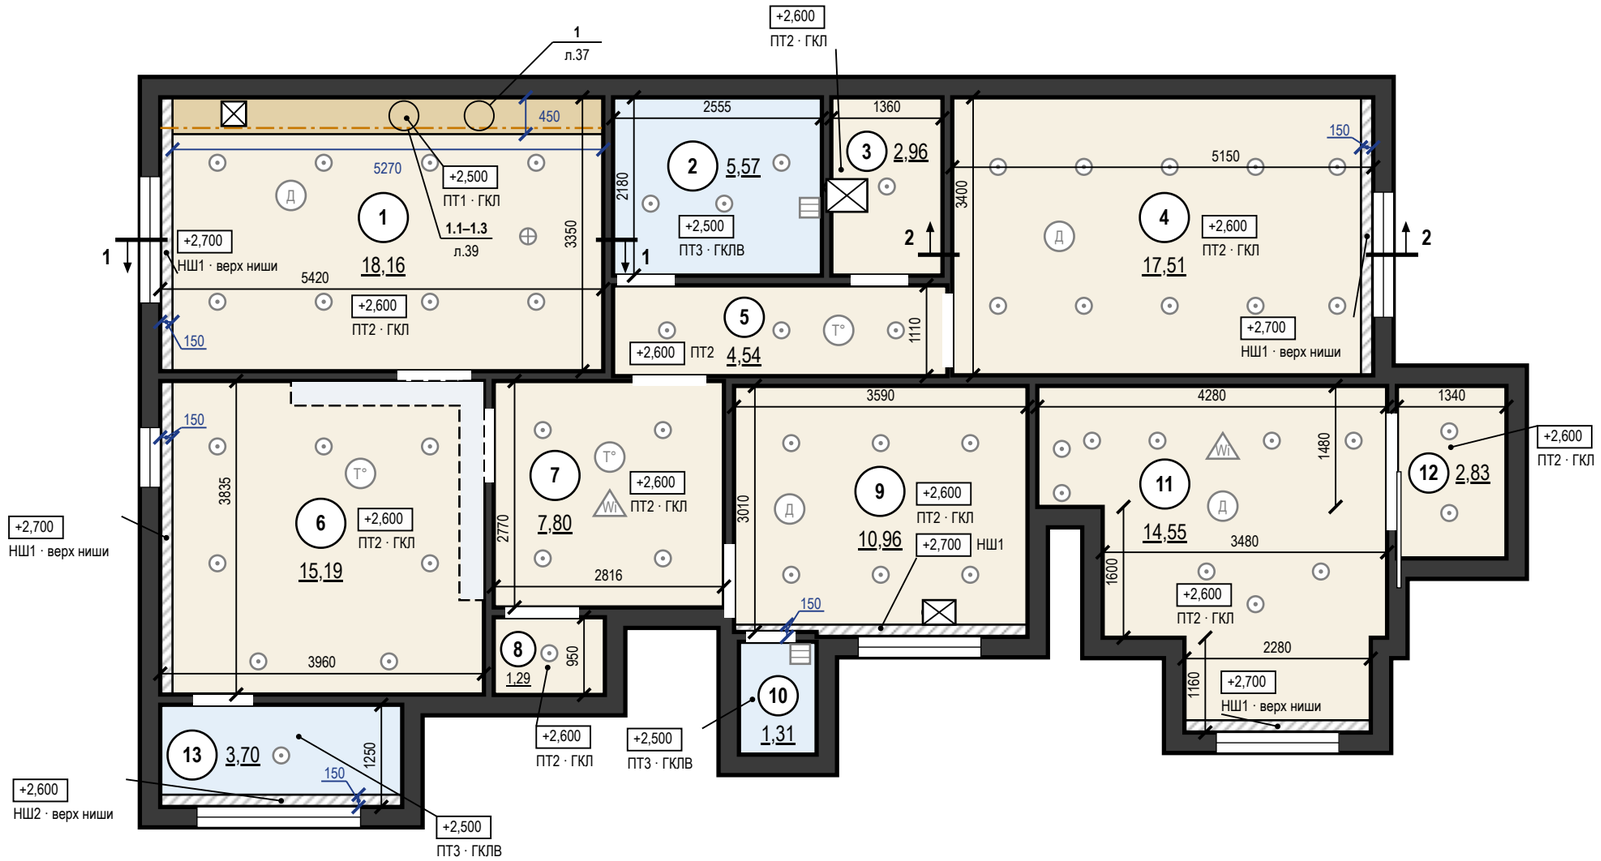

Ведомость потолков

Пом.	Марка	Конструкция	Низ / верх ниши	S, м²	Q
1	ПТ1	ГКЛ П113, короб LED	+2,500	2,37	Q3
1	ПТ2	ГКЛ П113	+2,600	15,29	Q3
1	НШ1	ниша под шторы 150×100	+2,700	0,50	
2	ПТ3	ГКЛВ П113	+2,500	5,57	Q3
3	ПТ2	ГКЛ П113	+2,600	2,96	Q3
4	ПТ2	То же	+2,600	17,00	Q3
4	НШ1	ниша под шторы 150×100	+2,700	0,51	
5	ПТ2	ГКЛ П113	+2,600	4,54	Q3
6	ПТ2	То же	+2,600	14,61	Q3
6	НШ1	ниша под шторы 150×100	+2,700	0,58	
7	ПТ2	ГКЛ П113	+2,600	7,80	Q3
8	ПТ2	То же	+2,600	1,29	Q3
9	ПТ2	То же	+2,600	10,48	Q3
9	НШ1	ниша под шторы 150×100	+2,700	0,48	
10	ПТ3	ГКЛВ П113	+2,500	1,31	Q3
11	ПТ2	ГКЛ П113	+2,600	14,21	Q3
11	НШ1	ниша под шторы 150×100	+2,700	0,34	
12	ПТ2	ГКЛ П113	+2,600	2,83	Q3
13	ПТ3	ГКЛВ П113	+2,500	3,26	Q3
13	НШ2	ниша под шторы 150×100	+2,600	0,44	
		Итого		**106,37**	

Ведомость вырезов и закладных в потолке

Марка	Устройство	Кол.	Пом.
	Светильник встраиваемый (марки — план освещения)	56	1, 2, 3, 4, 5, 6, 7, 8, 9, 10, 11, 12, 13
	Светильник подвесной (марки — план освещения)	1	1
ИП1, ИП2, ИП6, ИП7	Извещатель дымовой	4	1, 4, 9, 11
ИП3…ИП5	Извещатель тепловой	3	5, 6, 7
АР1, АР2	Точка доступа Wi-Fi, PoE	2	7, 11
ВР1, ВР3	Решётка вытяжная (вентилятор)	2	2, 10
	Люк ревизии 500×400, 400×300, 300×300	3	1, 3, 9

Примечания


1. За отметку ±0,000 принят уровень чистого пола сухих помещений (готовое покрытие), а не существующего пола; пол пом. 2, 10, 13 — −0,015, −0,030; верх плиты перекрытия −0,170 — расчётный по пирогу пола, не замерен; существующий пол снимается до плиты, его отметка не замерена. Отметки в прямоугольниках — низ потолка; низ плиты +2,700, +2,600. Марка потолка — одна конструкция и отметка на весь альбом.
2. Размеры помещений в свету (ширина × длина, мм), не поместившиеся на плане: пом. 3 — 1360 × 2180; пом. 5 — 4090 × 1110; пом. 8 — 1360 × 950; пом. 9 — 3590 × 3010, 2580 × 60; пом. 10 — 950 × 1380; пом. 12 — 1340 × 2110; пом. 13 — 2960 × 1250.
3. Потолки ГКЛ — каркасная система П113: подвесы через 1000 (с запасом: СП 163, табл. 14 — до 1100 при 0,15 кН/м²), несущие профили через 500, основные через 1200 мм; листы — поперёк несущих профилей. В помещениях 2, 10, 13 — ГКЛВ на оцинкованном каркасе.
4. LED-лента в алюминиевом профиле посередине карниза короба шириной 450 мм (узел 1, лист 37); длина по плану: пом. 1 — 5,4 м (в плане освещения 5,4).
5. Ниши под шторы 150×100 мм — на всю длину стены с окном; карниз — на закладной до обшивки (узел 2, лист 37).
6. Примыкание к стенам: теневой шов 15 мм, техзазор 3 мм — пом. 1, по стенам, выровненным штукатуркой (узел 1); пом. 2, 3, 4, 5, 6, 7, 8, 9, 10, 11, 12, 13 — разделительная лента.
7. Светильники и потолочные устройства — подложка с планов освещения, слаботочных систем и вентиляции (положение — по ним); вырезы и закладные — по ведомости на листе, до обшивки; отверстия не совмещать с профилями, глубина корпуса светильника до 70 мм.
8. Разрезы 1–1, 2–2 — на листе 37; высоты мебели и дверных блоков сверены с низом потолка в разрезах.
9. Шпаклевание ГКЛ и условия приёмки — Q3: рассеянный дневной свет, осмотр с 2 м; боковой свет не оценивается.
10. Пом. 6: короб воздуховода кухонной вытяжки ГКЛ 300×200 мм (ширина от стены × высота), низ +2,500, длина 4,44 м — по трассе плана вентиляции, вдоль стен до входа в канал под воздуховод Ø125; каркас ПН 28×27 по стене и плите, ПП 60×27, лист ГКЛ 12,5.
11. Люки ревизии 500×400, 400×300, 300×300 мм — по центру блоков питания LED (ревизия, ревизия, блок питания LED БП1; координаты — план освещения).
12. Сечения потолков М 1:10: пом. 4 — 4.1, 4.2 (лист 39); пом. 6 — 4.1, 4.2 (лист 39); пом. 9 — 4.1, 4.2 (лист 39); пом. 11 — 4.1, 4.2 (лист 39); пом. 13 — 13.1, 13.2 (листы 39, 40).

					Проект: Четырёхкомнатная квартира — **М 1:75**
	Лист	№ док.	Подпись	Дата	
Дизайнер	Кырлан А.С.			04.11.26	План потолков

Стадия	Лист	Листов
П	36	120


Разрез 1–1 (М 1:40)

Пом. 1 Зал; линия разреза — план потолков, лист 36

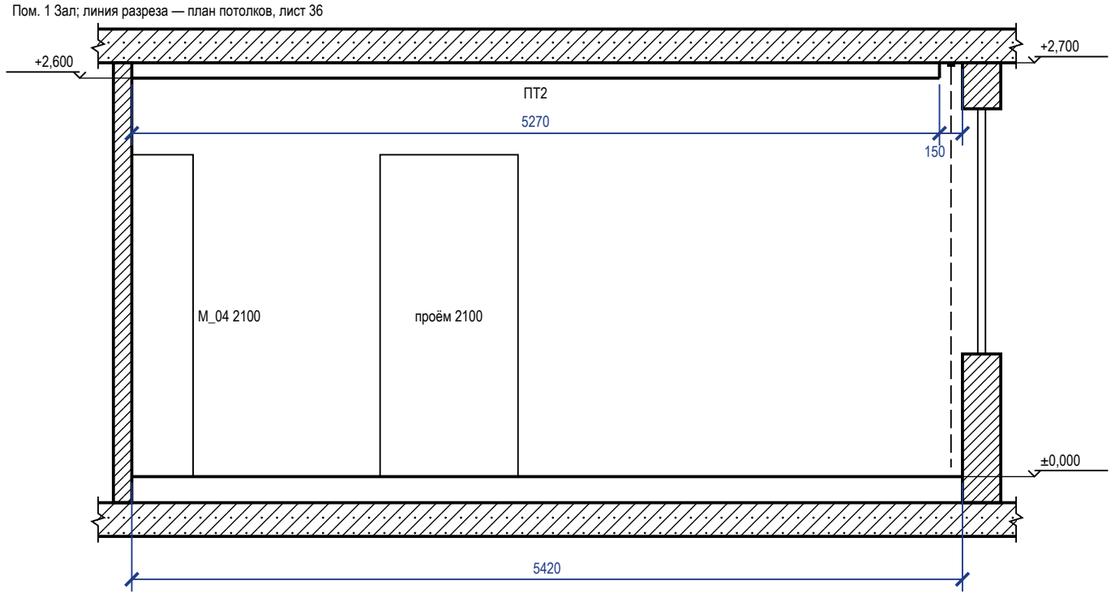


Разрез 2–2 (М 1:40)

Пом. 4 Детская 1; линия разреза — план потолков, лист 36

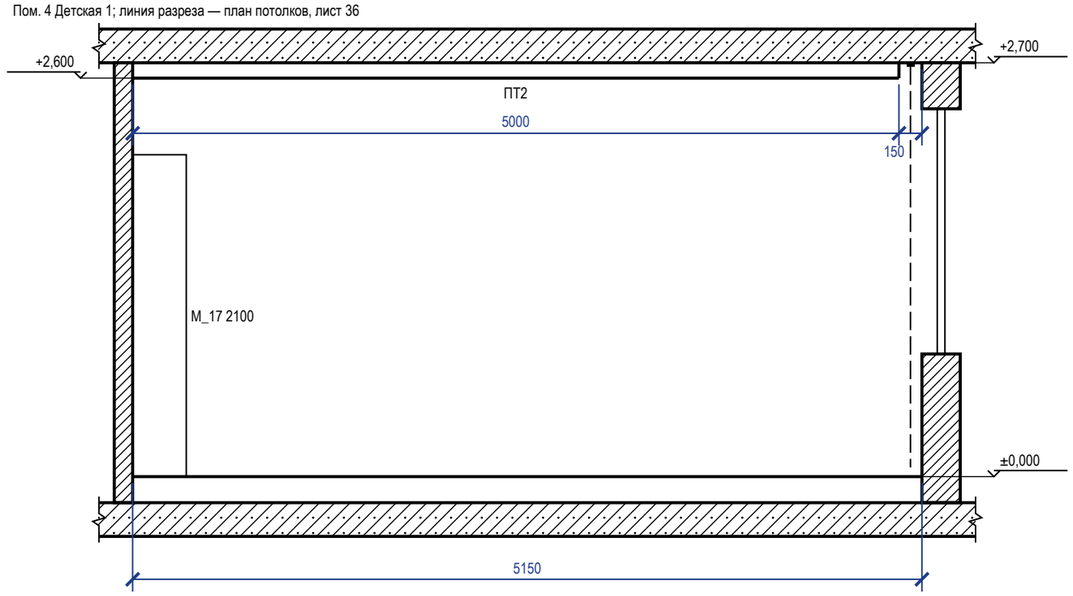

1 Короб с LED-подсветкой, теневой шов (М 1:10)


Пом. 1; карниз 150×100, щель под свет 60 мм

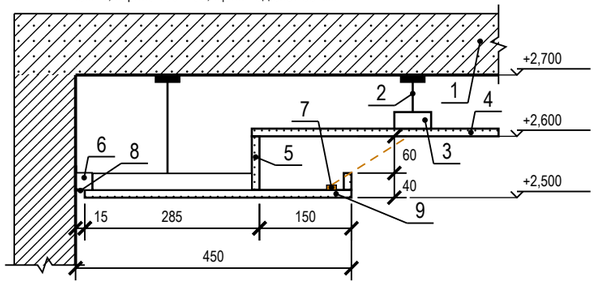

1 — плита перекрытия
2 — подвес прямой, шаг 1000 мм
3 — ПП 60×27: несущие через 500, основные через 1200 мм
4 — ГКЛ 12,5 по П113 — верхний уровень
5 — задняя стенка и бортик карниза — ГКЛ 12,5
6 — ПН 28×27 по периметру, к стене через 500 мм
7 — LED-лента в алюминиевом профиле
8 — теневой профиль: шов 15 мм, зазор 3 мм
9 — низ короба — ГКЛ 12,5 по ПП 60×27

2 Ниша под шторы (М 1:10)

Пом. 1, 4, 6, 9, 11, 13; без подсветки; закладные под карниз — до обшивки

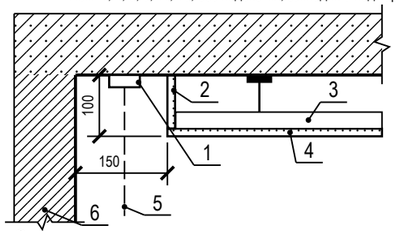

1 — карниз (шина), высота с верхом портьеры 80 мм
2 — стенка ниши — ГКЛ 12,5
3 — ПП 60×27 — каркас короба
4 — низ короба нижнего уровня — ГКЛ 12,5
5 — портьера
6 — стена с окном

Отметки по помещениям, м

Пом.	низ потолка	верх ниши	низ плиты
1, 4, 6, 9, 11	+2,600	+2,700	+2,700
13	+2,500	+2,600	+2,600

Условные обозначения

- плита перекрытия в сечении
- стена в сечении
- потолок ГКЛ в сечении; под линией — марка потолка (план потолков)
- мебель и дверные проёмы за секущей плоскостью; число — марка и верх от чистого пола, мм
- портьера в нише под шторы

Примечания

1. Разрезы — по линиям 1–1, 2–2 на плане потолков (лист 36). Отметки — от ±0,000 чистого пола, м; размеры — мм.
2. Высоты мебели и дверных блоков за секущей плоскостью сверены с низом потолка над ними: верх ниже низа короба и поля.
3. ГКЛ 12,5 мм по каркасу П113; перепад уровней и бортик карниза — ГКЛ по ПП 60×27 (узел 1 — на этом листе). Ниша под шторы — на всю длину стены с окном, карниз на закладной до обшивки (узел 2 — на этом листе).
4. Толщины плит перекрытия и пирога пола показаны условно.
5. Сечения потолков по помещениям М 1:10 (отметки помещения, профили, подвесы, крепёж, изделия) — листы 39–40.
6. Ведомость объёмов потолков (лист ГКЛ, профиль, подвесы, лента, блоки питания, люки) — на листе 38.

					Проект: Четырёхкомнатная квартира — М 1:40; 1:10
	Лист	№ док.	Подпись	Дата	
Дизайнер	Кырлан А.С.			04.11.26	Разрезы и узлы потолков

Стадия	Лист	Листов
П	37	120

Ведомость объёмов потолков

Позиция	Ед.	Кол.	Пом.
Лист ГКЛ 12,5	м²	98,99	1, 3, 4, 5, 6, 7, 8, 9, 11, 12
Лист ГКЛВ 12,5	м²	10,88	2, 10, 13
Борта и карнизы (входят в площади листов выше)	м²	3,50	1, 4, 6, 9, 11, 13
Профиль ПП 60×27	м	307,26	1, 2, 3, 4, 5, 6, 7, 8, 9, 10, 11, 12, 13
Профиль ПН 28×27	м	198,10	1, 2, 3, 4, 5, 6, 7, 8, 9, 10, 11, 12, 13
Подвес прямой	шт.	102	1, 2, 3, 4, 5, 6, 7, 8, 9, 10, 11, 12, 13
Анкер-клин к плите	шт.	102	1, 2, 3, 4, 5, 6, 7, 8, 9, 10, 11, 12, 13
Шуруп TN 3,5×25	шт.	2527	1, 2, 3, 4, 5, 6, 7, 8, 9, 10, 11, 12, 13
Лента армирующая для швов	м	131,84	1, 2, 3, 4, 5, 6, 7, 8, 9, 10, 11, 12, 13
Шпаклёвка для швов	кг	43,95	1, 2, 3, 4, 5, 6, 7, 8, 9, 10, 11, 12, 13
Грунтовка (швы)	л	10,99	1, 2, 3, 4, 5, 6, 7, 8, 9, 10, 11, 12, 13
Лента разделительная по периметру	м	143,31	1, 2, 3, 4, 5, 6, 7, 8, 9, 10, 11, 12, 13
Сплошная шпаклёвка и окраска (площадь развёртки)	м²	109,87	1, 2, 3, 4, 5, 6, 7, 8, 9, 10, 11, 12, 13
Лента LED	м	5,42	1
Требуемая мощность блоков питания	Вт	68	1
Установленная мощность блоков питания	Вт	100	1
Блок питания LED	шт.	1	1
Люк ревизии	шт.	3	1, 3, 9


Примечания

1. ГКЛ 12,5 мм по каркасу П113; узлы коробов и ниш под шторы: узел 1 — лист 37; узел 2 — лист 37; условные обозначения разрезов — на листе 37.
2. Ведомость объёмов — по геометрии плана потолков: Лист ГКЛ 12,5 — плоскости уровней + борта (без арочных участков); Лист ГКЛВ 12,5 — плоскости уровней + борта; Борта и карнизы — длина перепада × перепад; Профиль ПП 60×27 — S × (1/шаг несущ. + 1/шаг осн.) + стойки бортов; Профиль ПН 28×27 — периметр стен + 2 × перепады + карнизы; Подвес прямой — по раскладке: S уровня / (шаг осн. × шаг подвесов), пояс уже шага — ряд вдоль пояса, фигура — по контуру; шаг подвесов — не больше табл. 14 СП 163; Анкер-клин к плите — по одному на подвес (Knauf П113); Шуруп TN 3,5×25 — 23 шт./м² (Knauf П113, табл. 2 альбома П 11); Лента армирующая для швов — 1,2 м/м² листа (Knauf); Шпаклёвка для швов — 0,4 кг/м² листа, только швы (Knauf); Грунтовка (швы) — 0,1 л/м² листа, только швы (Knauf); Лента разделительная по периметру — периметр стен под потолком ГКЛ; Сплошная шпаклёвка и окраска (площадь развёртки) — плоскости + борта; расход — по паспорту материала (норма расхода на сплошной слой не подтверждена); Лента LED — по оси карниза и ниши фигуры (план потолков); Требуемая мощность блоков питания — Вт/м × длина × 1,3; Установленная мощность блоков питания — сумма мощностей блоков по плану освещения; Блок питания LED — блоки потолочных лент по плану освещения (БП1); Люк ревизии — план потолков; без запаса на подрезку (при закупке листа: ×1,075 при S > 20 м², ×1,175 — 10–20 м², ×1,275 — < 10 м²).

					Проект: Четырёхкомнатная квартира
	Лист	№ док.	Подпись	Дата	
Дизайнер	Кырлан А.С.			04.11.26	Разрезы и узлы потолков (продолжение)
					Стадия: П; Лист: 38; Листов: 120

Сечение 1.1. Короб с LED-подсветкой, теневой шов (М 1:10)


Пом. 1 Зал; карниз 150×100, щель под свет 60 мм

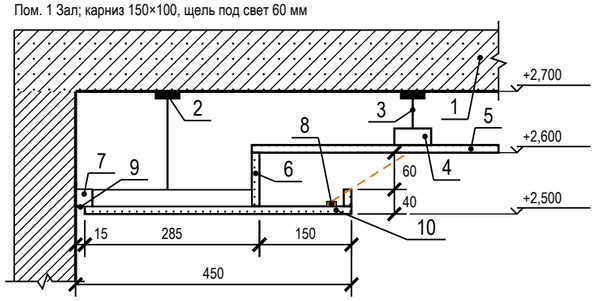

1 — плита перекрытия
2 — анкер-клин к плите — по одному на подвес
3 — подвес прямой, шаг 1000 мм
4 — ПП 60×27: несущие через 500, основные через 1200 мм; соединители одноуровневые, шурупы LN 3,5×9
5 — ГКЛ 12,5 по П113 — верхний уровень; шурупы TN 3,5×25 через 170 мм
6 — задняя стенка и бортик карниза — ГКЛ 12,5
7 — ПН 28×27 по периметру — дюбель-гвоздь через ≤ 500 мм, не менее 3 на профиль
8 — LED-лента 9,6 Вт/м, 24 В в алюминиевом профиле
9 — теневой профиль: шов 15 мм, зазор 3 мм
10 — низ короба — ГКЛ 12,5 по ПП 60×27

Сечение 1.2. Ниша под шторы (М 1:10)


Пом. 1 Зал; без подсветки; закладные под карниз — до обшивки

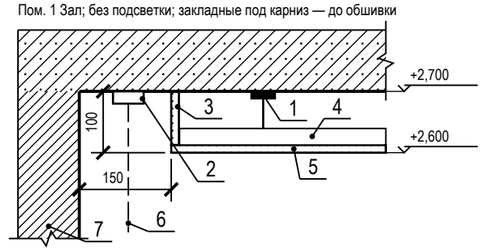

1 — анкер-клин к плите — по одному на подвес; подвес прямой, шаг 1000 мм
2 — карниз (шина), высота с верхом портьеры 80 мм
3 — стенка ниши — ГКЛ 12,5
4 — ПП 60×27 — каркас короба, основные через 1200 мм; соединители одноуровневые, шурупы LN 3,5×9
5 — низ короба нижнего уровня — ГКЛ 12,5; шурупы TN 3,5×25 через 170 мм
6 — портьера
7 — стена с окном

Сечение 1.3. Примыкание потолка к стене (М 1:10)


Пом. 1 Зал; примыкание — разделительная лента

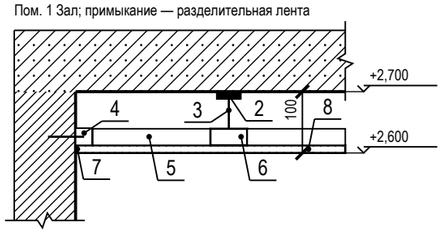

1 — плита перекрытия
2 — анкер-клин к плите — по одному на подвес
3 — подвес прямой, шаг 1000 мм
4 — ПН 28×27 по периметру — дюбель-гвоздь через ≤ 500 мм, не менее 3 на профиль
5 — ПП 60×27 несущий (вид) через 500 мм, в ПН
6 — ПП 60×27 основной (сечение) через 1200 мм; соединители одноуровневые, шурупы LN 3,5×9
7 — лента разделительная по стене, шов зашпаклёван
8 — ГКЛ 12,5 по П113; шурупы TN 3,5×25 через 170 мм

Сечение 4.1. Ниша под шторы (М 1:10)


Пом. 4 Детская 1, 6 Кухня, 9 Детская 2, 11 Гостиная; без подсветки; закладные под карниз — до обшивки

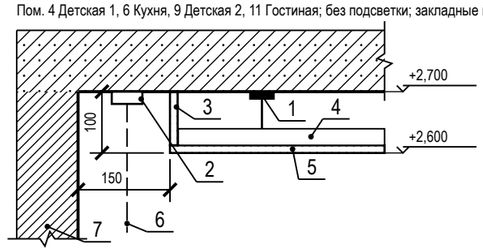

1 — анкер-клин к плите — по одному на подвес; подвес прямой, шаг 1000 мм
2 — карниз (шина), высота с верхом портьеры 80 мм
3 — стенка ниши — ГКЛ 12,5
4 — ПП 60×27 — каркас короба, основные через 1200 мм; соединители одноуровневые, шурупы LN 3,5×9
5 — низ короба нижнего уровня — ГКЛ 12,5; шурупы TN 3,5×25 через 170 мм
6 — портьера
7 — стена с окном

Сечение 4.2. Примыкание потолка к стене (М 1:10)


Пом. 4 Детская 1, 6 Кухня, 9 Детская 2, 11 Гостиная; примыкание — разделительная лента

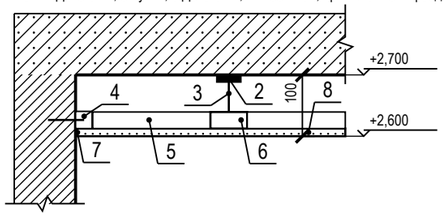

1 — плита перекрытия
2 — анкер-клин к плите — по одному на подвес
3 — подвес прямой, шаг 1000 мм
4 — ПН 28×27 по периметру — дюбель-гвоздь через ≤ 500 мм, не менее 3 на профиль
5 — ПП 60×27 несущий (вид) через 500 мм, в ПН
6 — ПП 60×27 основной (сечение) через 1200 мм; соединители одноуровневые, шурупы LN 3,5×9
7 — лента разделительная по стене, шов зашпаклёван
8 — ГКЛ 12,5 по П113; шурупы TN 3,5×25 через 170 мм

Сечение 13.1. Ниша под шторы (М 1:10)

Пом. 13 Балкон 1; без подсветки; закладные под карниз — до обшивки

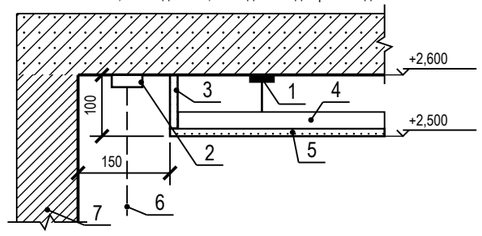

1 — анкер-клин к плите — по одному на подвес; подвес прямой, шаг 1000 мм
2 — карниз (шина), высота с верхом портьеры 80 мм
3 — стенка ниши — ГКЛВ 12,5
4 — ПП 60×27 — каркас короба, основные через 1200 мм; соединители одноуровневые, шурупы LN 3,5×9
5 — низ короба нижнего уровня — ГКЛВ 12,5; шурупы TN 3,5×25 через 170 мм
6 — портьера
7 — стена с окном

Условные обозначения

— · — LED-лента в нише подсветки (карниз короба, ниша фигуры)


Примечания

1. Сечения потолков М 1:10 по помещениям с нишами LED и нишами под шторы: отметки и размеры этого помещения от ±0,000 чистого пола (м, мм). Положение — по плану потолков (лист 36): короб и ниша LED — по линиям ленты, ниша под шторы — у стены с окном; типовые узлы по группам помещений — на листе 37.
2. Крепёж: подвес прямой к плите на анкер-клине — по одному на подвес (Knauf П113); ПН к стенам — дюбель-гвоздь через ≤ 500 мм, не менее 3 на профиль (серия 1.045.9-2.08); лист 12,5 — шурупы TN 3,5×25 через 170 мм (СП 163, табл. 15); профили между собой — соединители одноуровневые, шурупы LN 3,5×9.
3. Изделие карниза, профиля LED и галтели подписано артикулом из данных; где артикул не выбран, сечение дано по габаритам из данных (ширина и глубина ниши, щель под свет), изделие подбирается по ним.

					Проект: Четырёхкомнатная квартира			М 1:10
	Лист	№ док.	Подпись	Дата	Сечения потолков М 1:10	Стадия	Лист	Листов
Дизайнер	Кырлан А.С.			04.11.26		П	39	120

Сечение 13.2. Примыкание потолка к стене (М 1:10)

Пом. 13 Балкон 1; примыкание — разделительная лента

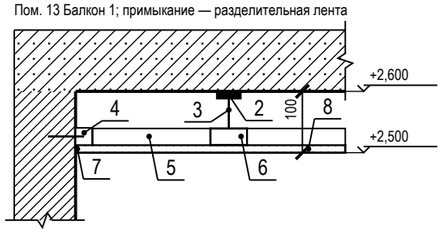

1 — плита перекрытия

2 — анкер-клин к плите — по одному на подвес

3 — подвес прямой, шаг 1000 мм

4 — ПН 28×27 по периметру — дюбель-гвоздь через ≤ 500 мм, не менее 3 на профиль

5 — ПП 60×27 несущий (вид) через 500 мм, в ПН

6 — ПП 60×27 основной (сечение) через 1200 мм; соединители одноуровневые, шурупы LN 3,5×9


7 — лента разделительная по стене, шов зашпаклёван

8 — ГКЛВ 12,5 по П113; шурупы TN 3,5×25 через 170 мм

Примечания

1. Сечения потолков М 1:10 по помещениям с нишами LED и нишами под шторы: отметки и размеры этого помещения от ±0,000 чистого пола (м, мм). Положение — по плану потолков (лист 36): короб и ниша LED — по линиям ленты, ниша под шторы — у стены с окном; типовые узлы по группам помещений — на листе 37.
2. Крепёж: подвес прямой к плите на анкер-клине — по одному на подвес (Knauf П113); ПН к стенам — дюбель-гвоздь через ≤ 500 мм, не менее 3 на профиль (серия 1.045.9-2.08); лист 12,5 — шурупы TN 3,5×25 через 170 мм (СП 163, табл. 15); профили между собой — соединители одноуровневые, шурупы LN 3,5×9.
3. Изделия карнизов, профилей LED и галтелей — по артикулу из данных.

					Проект: Четырёхкомнатная квартира	М 1:10
	Лист	№ док.	Подпись	Дата	Сечения потолков М 1:10	Стадия / Лист / Листов
Дизайнер	Кырлан А.С.			04.11.26		П / 40 / 120

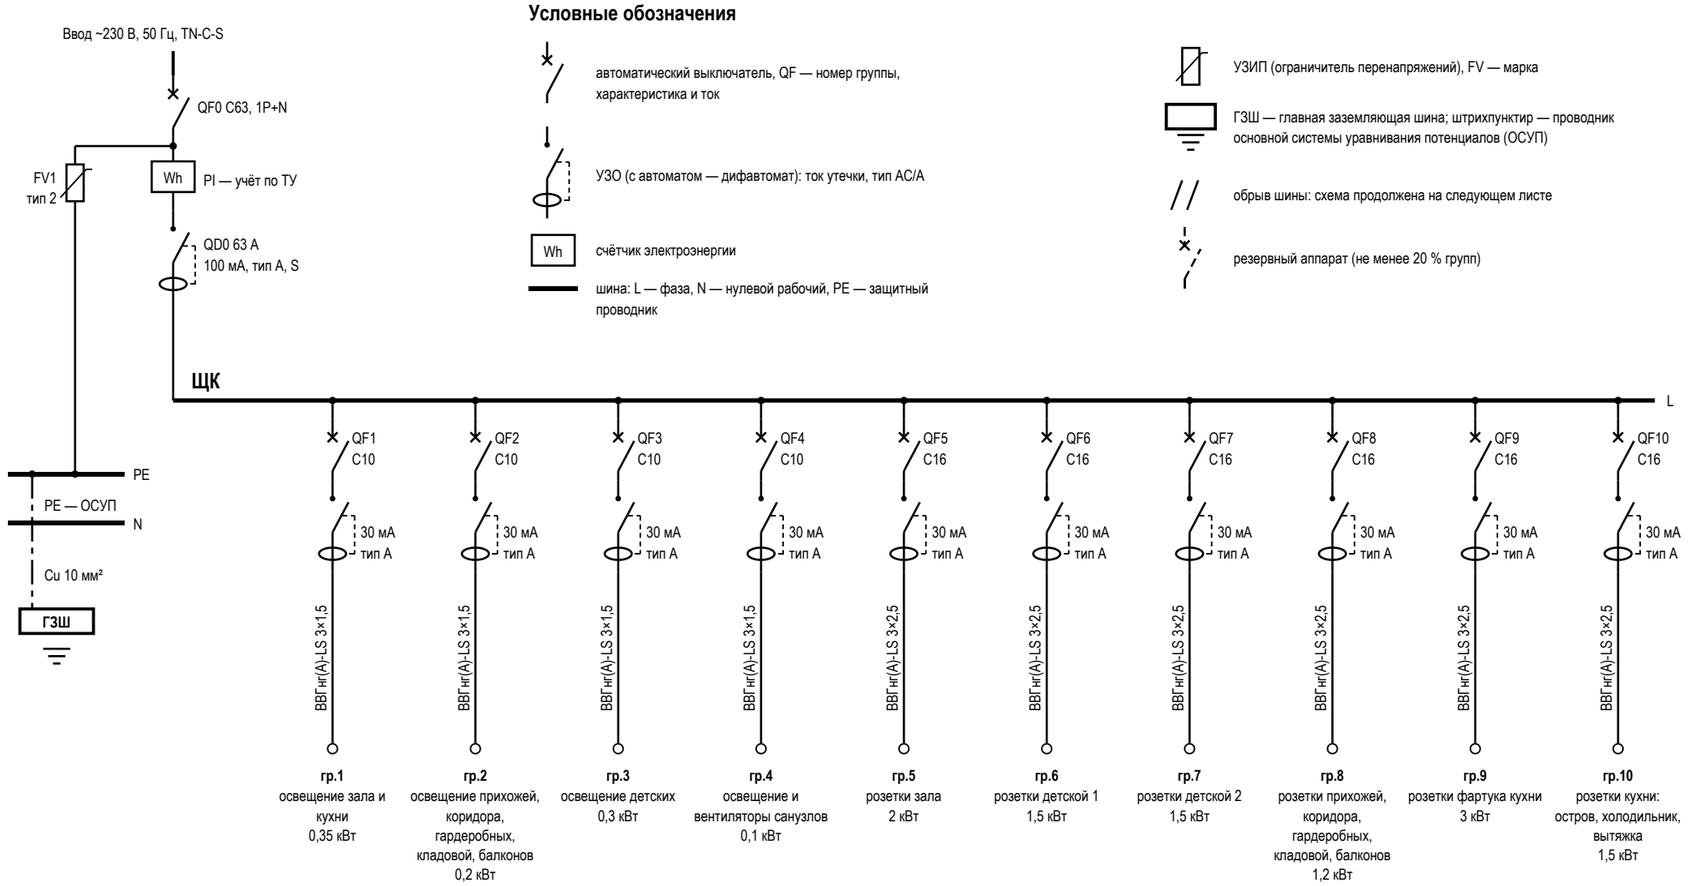

Условные обозначения

- автоматический выключатель, QF — номер группы, характеристика и ток
- УЗО (с автоматом — дифавтомат): ток утечки, тип AC/A
- Wh — счётчик электроэнергии
- шина: L — фаза, N — нулевой рабочий, PE — защитный проводник
- УЗИП (ограничитель перенапряжений), FV — марка
- ГЗШ — главная заземляющая шина; штрихпунктир — проводник основной системы уравнивания потенциалов (ОСУП)
- обрыв шины: схема продолжена на следующем листе
- резервный аппарат (не менее 20 % групп)

Данные щитка

Показатель	Значение
Номер щитка	ЩК
Тип	ЩРВ-П-72, IP41, навесной
Уст. мощность, кВт	29,75
Разреш. мощность, кВт	15
Расчётная, кВт	11,2
Автоматы 1п: занят. / рез.	19 / 4
Модулей: всего / занято	72 / 44
Ток на вводе, А	63
Вводной аппарат	QF0 C63, 1P+N
УЗИП	FV1, тип 2, ЩК, после счётчика
ГЗШ, проводник ОСУП	Cu 10 мм²
Листов схемы	2 (группы по листам)

Таблица групп щита ЩК и кабельный журнал

№	Назначение	Помещения	Автомат	УЗО / дифавтомат	Кабель	Длина, м	Р, кВт	Точек
1	освещение зала и кухни	1, 6	C10	30 мА, тип A	ВВГнг(A)-LS 3×1,5	55,5	0,35	25
2	освещение прихожей, коридора, гардеробных, кладовой, балконов	3, 5, 6, 7, 8, 12, 13	C10	30 мА, тип A	ВВГнг(A)-LS 3×1,5	111,7	0,2	20
3	освещение детских	4, 9, 11	C10	30 мА, тип A	ВВГнг(A)-LS 3×1,5	99,5	0,3	34
4	освещение и вентиляторы санузлов	2, 5, 10	C10	30 мА, тип A	ВВГнг(A)-LS 3×1,5	34,7	0,1	9
5	розетки зала	1	C16	30 мА, тип A	ВВГнг(A)-LS 3×2,5	27,6	2	6
6	розетки детской 1	4	C16	30 мА, тип A	ВВГнг(A)-LS 3×2,5	32,8	1,5	5
7	розетки детской 2	9	C16	30 мА, тип A	ВВГнг(A)-LS 3×2,5	24,1	1,5	4
8	розетки прихожей, коридора, гардеробных, кладовой, балконов	3, 5, 7, 12, 13	C16	30 мА, тип A	ВВГнг(A)-LS 3×2,5	72,9	1,2	6
9	розетки фартука кухни	6	C16	30 мА, тип A	ВВГнг(A)-LS 3×2,5	18,3	3	4
10	розетки кухни: остров, холодильник, вытяжка	6	C16	30 мА, тип A	ВВГнг(A)-LS 3×2,5	19,6	1,5	6

Примечания

1. Схема однолинейная: одна линия — фаза, N и PE группы; аппараты — в отключённом положении (ГОСТ 2.702, ГОСТ 2.755). Номера групп — как у точек на планах (гр.). За отметку 0,000 принят уровень чистого пола; высота щита — по плану розеток.
2. Розеточные и мокрые линии — через УЗО или дифавтомат с током утечки не более 30 мА (ПУЭ 7.1.79); в санузле выполнить ДСУП (ПУЭ 7.1.87–7.1.88).
3. УЗО тип A — для линий с электроникой, стиральной и посудомоечной машиной, LED-драйверами; тип AC — только для чисто активной нагрузки.
4. Кабель — медный, исполнение нг(A)-LS (ГОСТ 31565-2012); скрытая прокладка только горизонтально и вертикально, фактические трассы зафиксировать исполнительной схемой до закрытия отделкой.
5. Номинал автомата — не выше допустимого тока кабеля: 1,5 мм² — до 10 А, 2,5 мм² — до 16 А. Резерв щита — не менее 20 % модулей.
6. Расчёт нагрузок, токов КЗ, селективности и сечений — по проекту ЭОМ организации с допуском СРО; лист задаёт состав, расположение и группы.
7. УЗИП FV1 — после вводного автомата, проводник к шине PE — кратчайший, без петель. Шина PE щита соединяется с ГЗШ проводником ОСУП; к ГЗШ присоединяются трубы водопровода и отопления на вводе в квартиру (ПУЭ 7.1.87). Шины N и PE — раздельные, после разделения PEN не объединяются.
8. До подключения нагрузки — приёмо-сдаточные испытания с протоколом: сопротивление изоляции линий не менее 0,5 МОм, срабатывание УЗО по току и времени, непрерывность защитных проводников PE (ПУЭ, гл. 1.8).

					Проект: Четырёхкомнатная квартира
	Лист	№ док.	Подпись	Дата	Однолинейная схема щита
Дизайнер	Кырлан А.С.			04.11.26	

Стадия	Лист	Листов
П	41	120

Продолжение однолинейной схемы щита ЩК, начало — лист 41

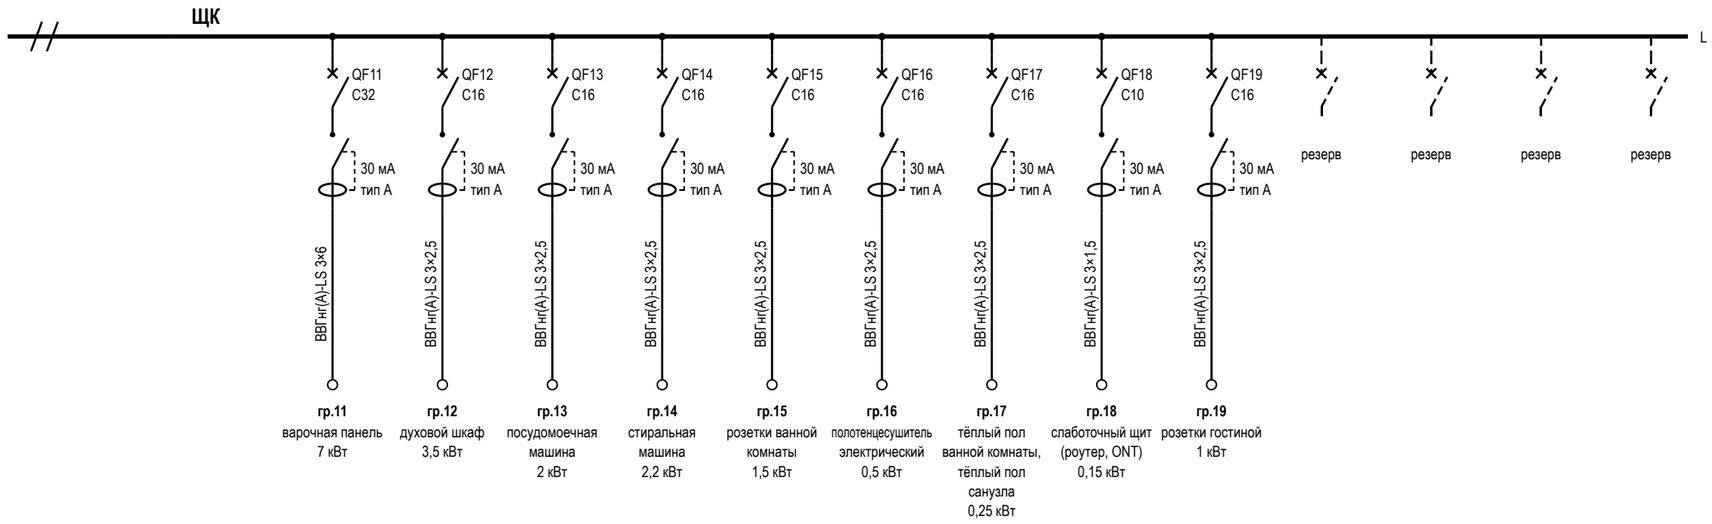



Таблица групп щита ЩК и кабельный журнал (продолжение)

№	Назначение	Помещения	Автомат	УЗО / дифавтомат	Кабель	Длина, м	Р, кВт	Точек
11	варочная панель	6	C32	30 мА, тип А	ВВГнг(А)-LS 3×6	9,8	7	1
12	духовой шкаф	6	C16	30 мА, тип А	ВВГнг(А)-LS 3×2,5	8,9	3,5	1
13	посудомоечная машина	6	C16	30 мА, тип А	ВВГнг(А)-LS 3×2,5	7,3	2	1
14	стиральная машина	2	C16	30 мА, тип А	ВВГнг(А)-LS 3×2,5	13,8	2,2	1
15	розетки ванной комнаты	2	C16	30 мА, тип А	ВВГнг(А)-LS 3×2,5	13,2	1,5	1
16	полотенцесушитель электрический	2	C16	30 мА, тип А	ВВГнг(А)-LS 3×2,5	15,7	0,5	1
17	тёплый пол ванной комнаты, тёплый пол санузла	2, 10	C16	30 мА, тип А	ВВГнг(А)-LS 3×2,5	24	0,25	2
18	слаботочный щит (роутер, ONT)	7	C10	30 мА, тип А	ВВГнг(А)-LS 3×1,5	6	0,15	1
19	розетки гостиной	11	C16	30 мА, тип А	ВВГнг(А)-LS 3×2,5	25,7	1	3
	Итого по сечениям ВВГнг(А)-LS (все группы щита), м: 3×1,5 — 307,4; 3×2,5 — 303,9; 3×6 — 9,8					621,1		

Примечания

1. Лист — продолжение однолинейной схемы щита ЩК: начало, данные щитка и условные обозначения — лист 41. Ввод, учёт, вводной аппарат, УЗИП, шины N и PE и ГЗШ показаны там же; шина L листа — та же шина щита.
2. Схема однолинейная: одна линия — фаза, N и PE группы; аппараты — в отключённом положении (ГОСТ 2.702, ГОСТ 2.755). Номера групп — как у точек на планах (гр.). За отметку 0,000 принят уровень чистого пола; высота щита — по плану розеток.
3. Розеточные и мокрые линии — через УЗО или дифавтомат с током утечки не более 30 мА (ПУЭ 7.1.79); в санузле выполнить ДСУП (ПУЭ 7.1.87–7.1.88).
4. УЗО тип А — для линий с электроникой, стиральной и посудомоечной машиной, LED-драйверами; тип АС — только для чисто активной нагрузки.
5. Кабель — медный, исполнение нг(А)-LS (ГОСТ 31565-2012); скрытая прокладка только горизонтально и вертикально, фактические трассы зафиксировать исполнительной схемой до закрытия отделкой.
6. Номинал автомата — не выше допустимого тока кабеля: 1,5 мм² — до 10 А, 2,5 мм² — до 16 А. Резерв щита — не менее 20 % модулей.
7. Расчёт нагрузок, токов КЗ, селективности и сечений — по проекту ЭОМ организации с допуском СРО; лист задаёт состав, расположение и группы.
8. До подключения нагрузки — приёмо-сдаточные испытания с протоколом: сопротивление изоляции линий не менее 0,5 МОм, срабатывание УЗО по току и времени, непрерывность защитных проводников PE (ПУЭ, гл. 1.8).

					Проект: Четырёхкомнатная квартира
	Лист	№ док.	Подпись	Дата	
Дизайнер	Кырлан А.С.			04.11.26	Однолинейная схема щита (продолжение)
					Стадия: П; Лист: 42; Листов: 120

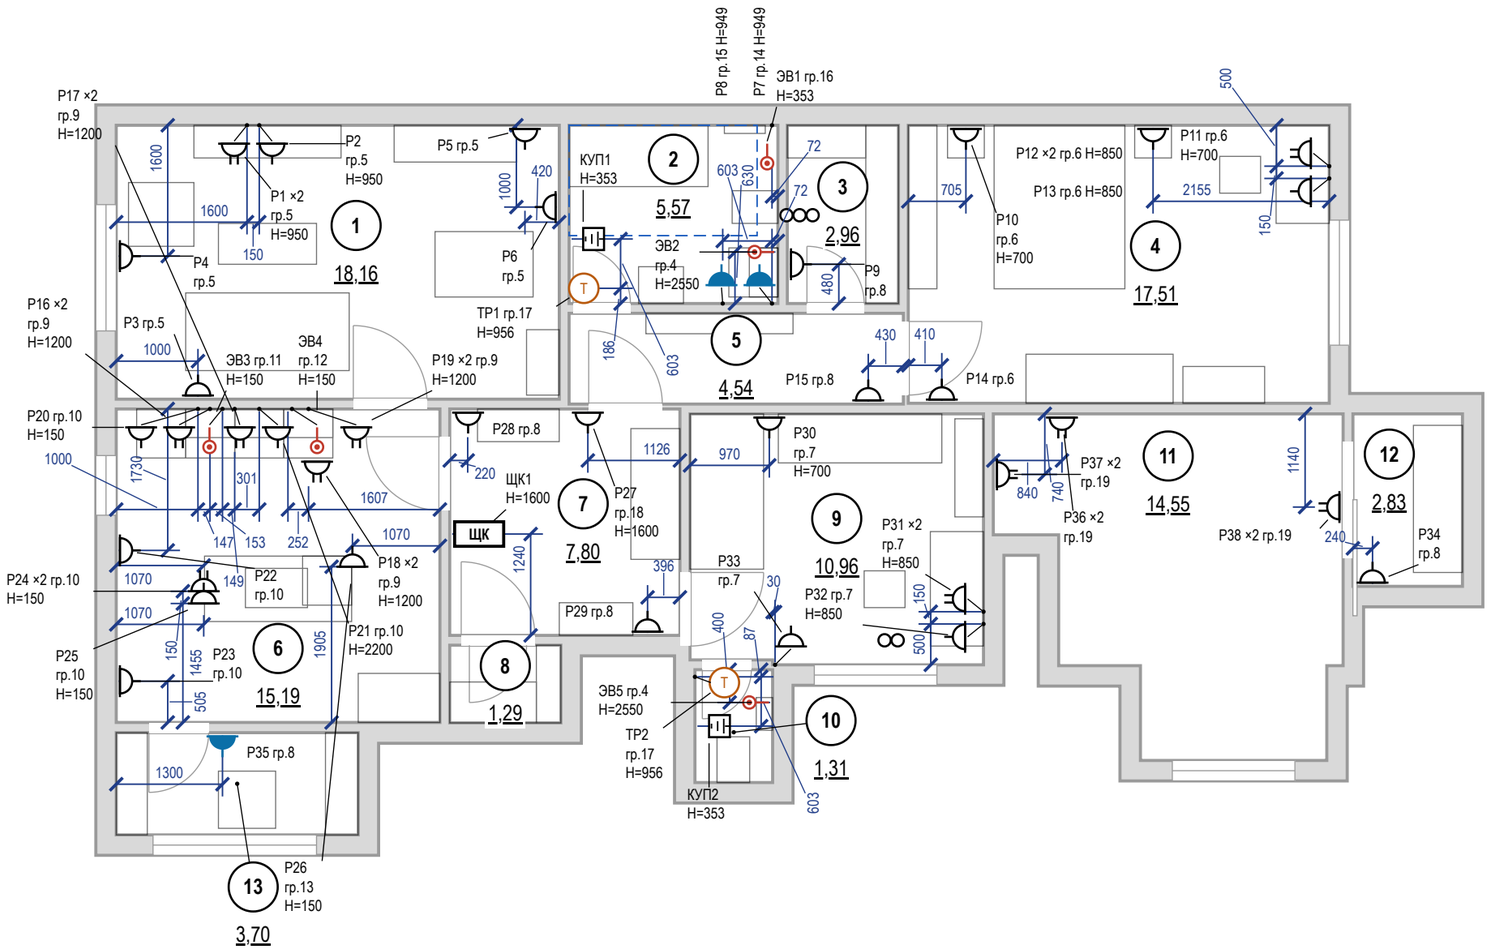

Условные обозначения

Знак	Тип изделия	Н, мм	Кол., шт
	Розетка с заземлением	300	13
	То же	у знака	11
	Блок розеток с заземлением, рамка 2 поста	300	3
	То же	у знака	8
	Розетка с заземлением IP44	300	1
	То же	у знака	2
	Вывод кабеля к прибору	у знака	5
	КУП (уравнивание потенциалов)	353	2
Т	Терморегулятор тёплого пола	956	2
ЩК	Щит квартирный	1600	1

розетка с заземляющим контактом; у знака — марка, ×N — постов в рамке, гр. — группа щита, Н — высота оси, мм

знак разведён для читаемости: точка на стене — у выноски, привязка — до неё

граница зоны 2 ванной (600 мм от ванны/поддона)

мебель и сантехприборы — подложка

стояк: К1 — канализация, В1 — ХВС, Т3 — ГВС

1 номер помещения, площадь м²


Итого розеток (механизмов) — 49 шт; рамок — 38 шт: на 1 пост — 27, на 2 поста — 11.

Примечания

1. За отметку 0,000 принят уровень чистого пола. Высоты Н — от чистого пола до оси изделия; привязки — от чистовой грани стены до оси механизма (у рамки на несколько постов — до оси рамки).
2. Розетки без отметки Н у знака — на высоте 300 мм от чистого пола до оси механизма; выводы кабеля — по паспорту прибора.
3. Розетки в санузле — только вне зон 0–2 (ПУЭ 7.1.48, ГОСТ Р 50571.7.701-2024), IP44, через УЗО 30 мА.
4. Розеточные и мокрые линии — через УЗО или дифавтомат с током утечки не более 30 мА (ПУЭ 7.1.79); в санузле выполнить ДСУП (ПУЭ 7.1.87–7.1.88).
5. Кабель — медный, исполнение нг(А)-LS (ГОСТ 31565-2012); скрытая прокладка только горизонтально и вертикально, фактические трассы зафиксировать исполнительной схемой до закрытия отделкой.
6. Расчёт нагрузок, токов КЗ, селективности и сечений — по проекту ЭОМ организации с допуском СРО; лист задаёт состав, расположение и группы.

					Проект: Четырёхкомнатная квартира — М 1:75
	Лист	№ док.	Подпись	Дата	
Дизайнер	Кырлан А.С.			04.11.26	План розеток и электровыводов

Стадия	Лист	Листов
П	43	120

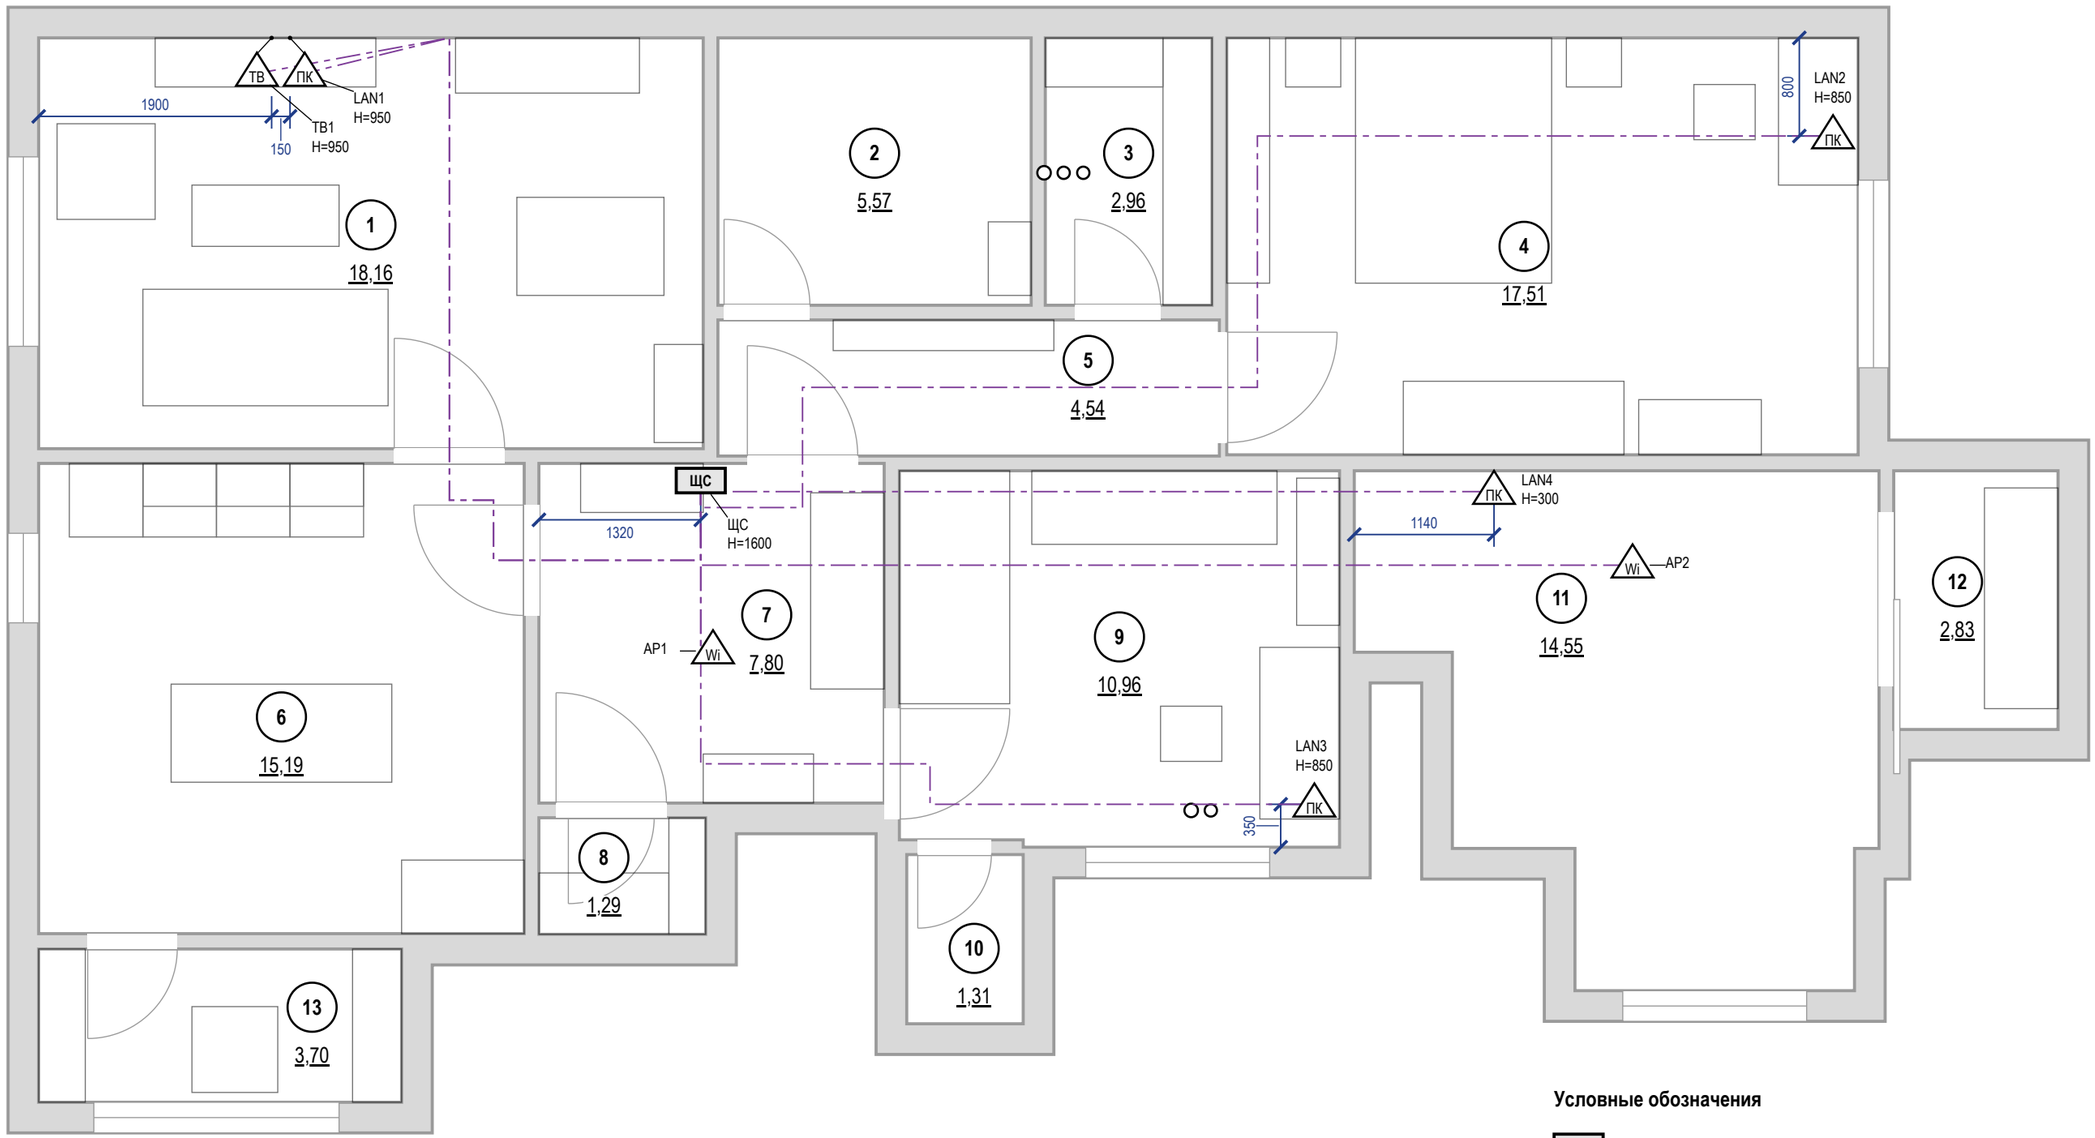

Условные обозначения

ЩС	щит слаботочный: ввод провайдера, роутер, коммутатор
ПК	розетка компьютерная RJ45
ТВ	розетка телевизионная
Wi	точка доступа Wi-Fi (питание PoE)
— — —	кабель от ЩС до точки, отдельным лучом
▭	мебель и сантехприборы — подложка
○	стояк: К1 — канализация, В1 — ХВС, Т3 — ГВС
1	номер помещения, площадь м²


Примечания

1. За отметку 0,000 принят уровень чистого пола. Высоты Н — от чистого пола до оси изделия; привязки — от чистовой грани стены до оси механизма (у рамки на несколько постов — до оси рамки).
2. Высота установки, не указанная на плане: розетки LAN и ТВ — 300 мм от чистого пола.
3. Слаботочные кабели — отдельно от силовых: в своей трубе или лотке, при параллельной прокладке не ближе 100 мм к силовым, пересечения под прямым углом; каждую точку — отдельным кабелем от ЩС без скруток.
4. Трассы на листе — принципиальные; фактические зафиксировать исполнительной схемой до закрытия отделкой. Силовые линии, УЗО 30 мА, ДСУП, кабель нг(А)-LS — по листам розеток и щита.
5. Проект силовой части и расчёт токов КЗ — по проекту ЭОМ; слаботочная часть согласуется с провайдером и управляющей компанией (домофон, коллективное ТВ).

					Проект: Четырёхкомнатная квартира	М 1:50
	Лист	№ док.	Подпись	Дата	План слаботочных сетей	Стадия / Лист / Листов
Дизайнер	Кырлан А.С.			04.11.26		П / 44 / 120

Условные обозначения

- светильник встраиваемый точечный
- Св1·L1 — марка светильника (как в ведомости и на развёртках) · группа включения L (лист 47)
- мебель и сантехприборы — подложка
- светильник подвесной
- Д — извещатель пожарный дымовой автономный
- стояк: К1 — канализация, В1 — ХВС, Т3 — ГВС
- светильник настенный (бра), Н — высота оси
- Т° — извещатель пожарный тепловой
- 1 — номер помещения, площадь м²
- светодиодная лента в профиле / в карнизе короба
- БП — блок питания LED, с доступом (люк от 100×100 мм)

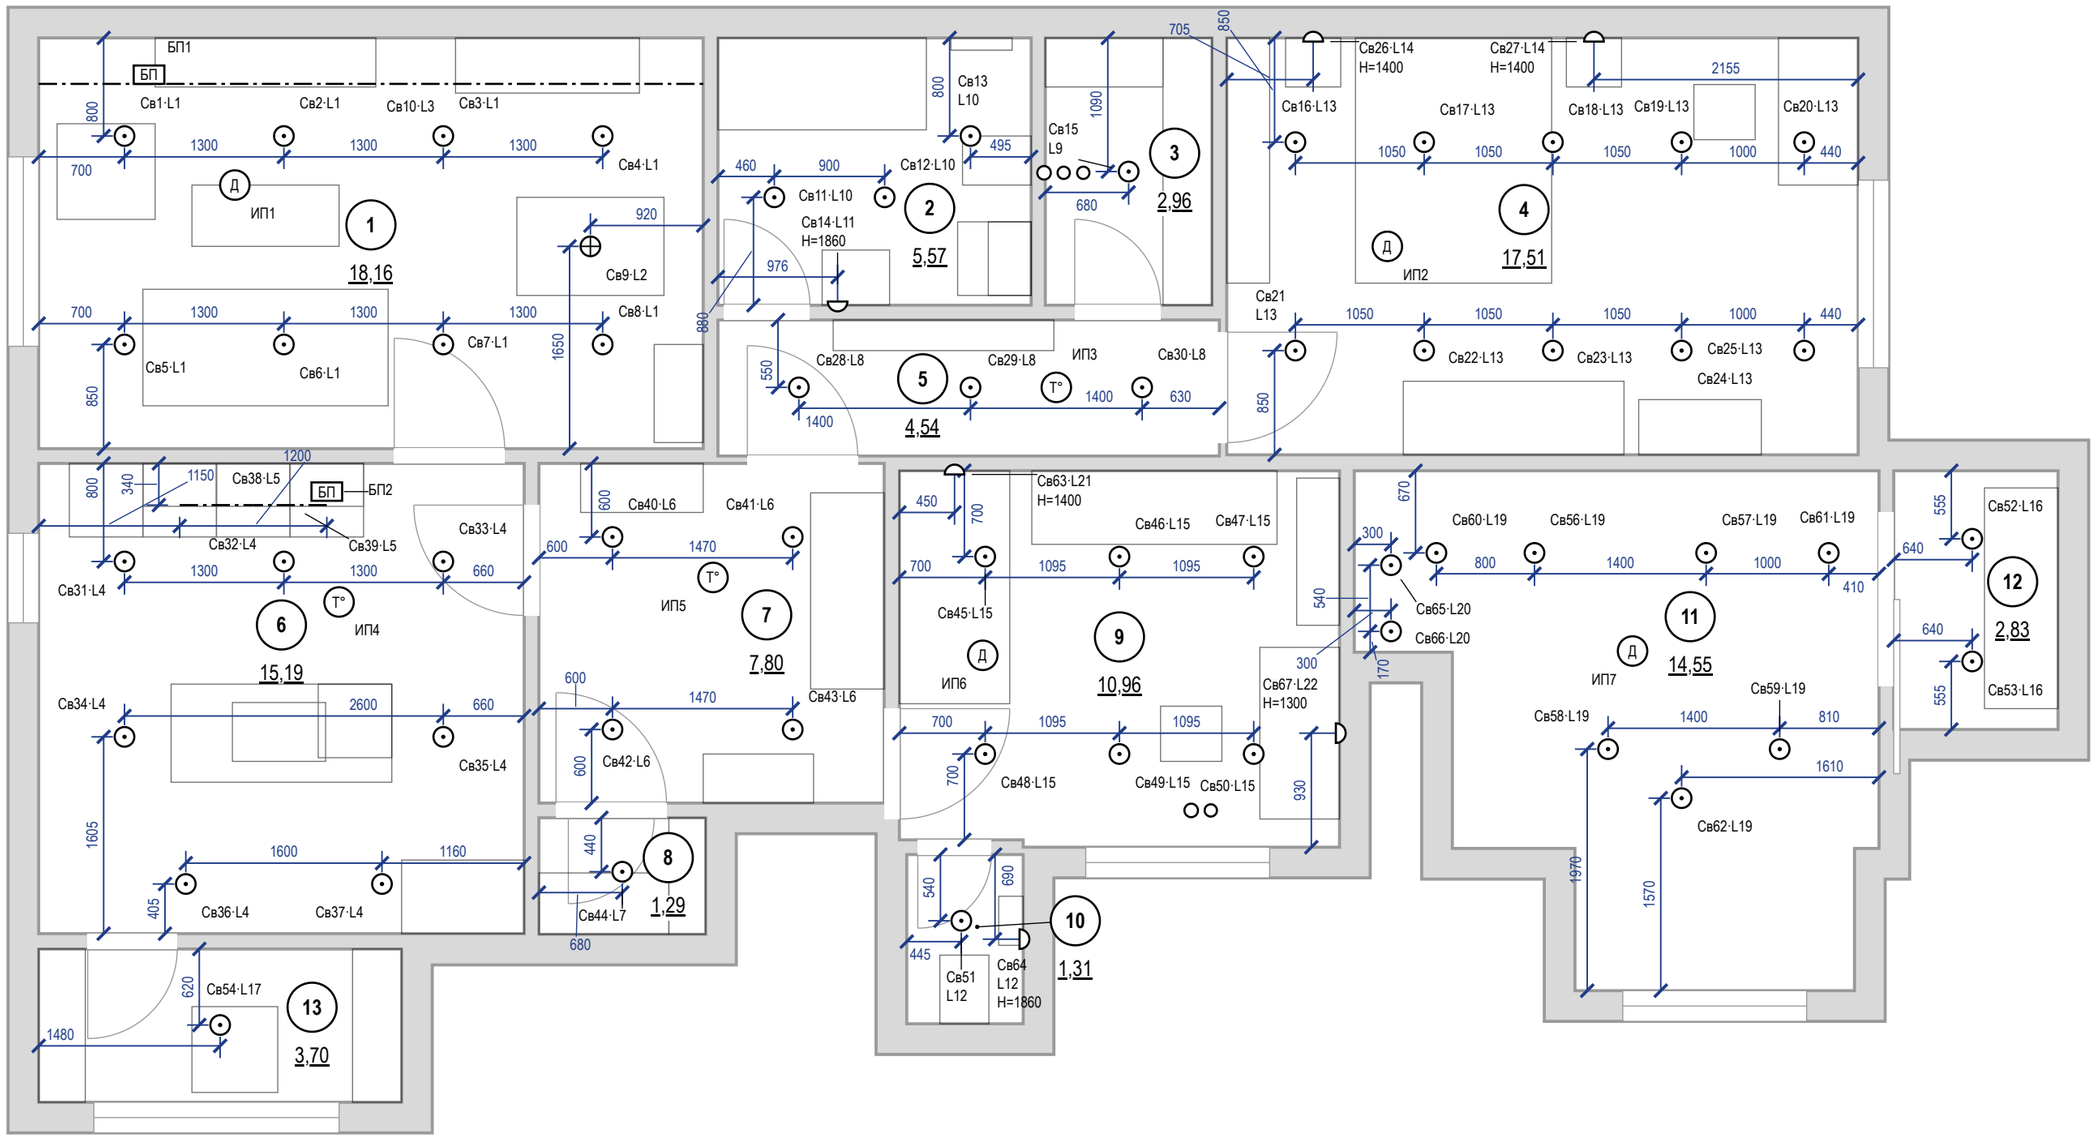

Примечания

1. За отметку 0,000 принят уровень чистого пола. Высоты Н — от чистого пола до оси изделия; привязки — от чистовой грани стены до оси механизма (у рамки на несколько постов — до оси рамки).
2. Высота установки, не указанная на плане: светильники — на потолке; настенные — по отметке Н у знака. Привязки — до оси светильника от чистовой грани стены, по рядам.
3. Во влажных помещениях — светильники не ниже IP44; в зонах 0–2 ванной — по ГОСТ Р 50571.7.701-2024 (зона 1 — IPX5).
4. LED-лента в карнизе подсветки короба — по линии карниза с плана потолков; блок питания — в люке короба (БП на плане), питание ленты длиннее 5 м — с двух концов.
5. Розеточные и мокрые линии — через УЗО или дифавтомат с током утечки не более 30 мА (ПУЭ 7.1.79); в санузле выполнить ДСУП (ПУЭ 7.1.87–7.1.88).
6. Кабель — медный, исполнение нг(А)-LS (ГОСТ 31565-2012); скрытая прокладка только горизонтально и вертикально, фактические трассы зафиксировать исполнительной схемой до закрытия отделкой.
7. Расчёт нагрузок, токов КЗ, селективности и сечений — по проекту ЭОМ организации с допуском СРО; лист задаёт состав, расположение и группы.
8. Ведомость светильников (тип, количество, мощность, поток, Tц, Ra) — лист 46.

					Проект: Четырёхкомнатная квартира — М 1:50
	Лист	№ док.	Подпись	Дата	
Дизайнер	Кырлан А.С.			04.11.26	План освещения
					Стадия: П; Лист: 45; Листов: 120

Параметры светильников для подбора

Поз.	Марки	Наименование	Установка	Кол.	P, Вт	Σ P, Вт	Ф, лм	Тц, К	Ra	Угол, °	IP	Дим.	Слой	Группа	Пом.
1	Св1–Св8, Св16–Св19, Св20, Св21–Св24, Св25, Св31–Св37, Св56–Св62	Встраиваемый точечный	в ГКЛ, корпус ≤ 70 мм	32	12	384	1000	3000	90	—	20	—	общий	L1, L4, L13, L19	1, 4, 6, 11
2	Св9	Подвесной	подвес, низ H=1600	1	15	15	1200	2700	90	—	20	—	рабочий	L2	1
3	Св10	Лента светодиодная 24 В	в карнизе короба, профиль с рассеивателем	5,4 м	9,6/м	52	900/м	2700	90	—	20	да	акцентный	L3	1
4	Св11, Св12, Св13, Св51	Встраиваемый точечный	в ГКЛ, корпус ≤ 70 мм	4	6	24	500	3000	90	—	44	—	общий	L10, L12	2, 10
5	Св14, Св64	Светильник над зеркалом, драйвер встроен	над зеркалом, H=1860	2	8	16	600	3000	90	—	44	—	рабочий	L11, L12	2, 10
6	Св15, Св40–Св44, Св52, Св53, Св65, Св66	Встраиваемый точечный	в ГКЛ, корпус ≤ 70 мм	10	6	60	500	3000	90	—	20	—	общий, акцентный	L6, L7, L9, L16, L20	3, 7, 8, 11, 12
7	Св26, Св27, Св63	Настенный (бра)	на стене, H=1400	3	6	18	400	2700	90	60	20	—	рабочий	L14, L21	4, 9
8	Св28–Св30	Встраиваемый точечный	в ГКЛ, корпус ≤ 70 мм	3	5	15	400	3000	90	—	20	—	общий	L8	5
9	Св38, Св39	Линейный светильник	на поверхности	1,2 м	8	16	700	3000	90	—	20	—	рабочий	L5	6
10	Св45–Св50	Встраиваемый точечный	в ГКЛ, корпус ≤ 70 мм	6	13	78	1100	3000	90	—	20	—	общий	L15	9
11	Св67	Бра подсветки рабочего места, стол M_35	на стене, H=1300	1	7	7	450	3000	90	60	20	—	рабочий	L22	9
12	Св54	Встраиваемый точечный	в ГКЛ, корпус ≤ 70 мм	1	9	9	800	3000	90	—	44	—	общий	L17	13
		Итого		**63 шт + 6,6 м**		**694**									

LED-ленты, линейные светильники и блоки питания

Марка	Пом.	L, м	U, В	Вт/м	Σ P, Вт	БП	P БП, Вт	Загр., %	Питание	Доступ к БП
Св10	1	5,4	24	9,6	52	БП1	100	52	с одного конца	люк 300×300 в коробе потолка у стены A
Св38	6	0,6	24	—	8	БП2	30	53	встроенный ввод	в навесном модуле M_25, съёмная панель
Св39	6	0,6	24	—	8	БП2	30	53	встроенный ввод	в навесном модуле M_25, съёмная панель

Сценарии (помещения со светорегуляторами)

Помещение	Сценарий	Горят группы (уровень)	Управление
1. Зал	Вечер	L2 подвес над обеденным столом — вкл.; L3 лента в карнизе (диммер) — 50 %; остальные выкл.	светорегулятор S2; выключатель S1
	Гости	L1 общий свет (споты) — вкл.; L2 подвес над обеденным столом — вкл.; L3 лента в карнизе (диммер) — 100 %	светорегулятор S2; выключатель S1
	Кино	L3 лента в карнизе (диммер) — 20 %; остальные выкл.	светорегулятор S2
	Уборка	L1 общий свет (споты) — вкл.; L2 подвес над обеденным столом — вкл.; остальные выкл.	выключатель S1


Примечания

1. Позиции и марки Св — те же, что на плане освещения (лист 45); группы L — по плану выключателей (лист 47).
2. Модели светильников не выбраны: лист — техническое задание на подбор. Модель по строке таблицы: поток, Тц, Ra, угол, IP и регулировка яркости не хуже указанных, мощность не больше; встраиваемые — под глубину короба (графа «Установка»). IP 20 — сухие помещения. После выбора моделей (артикул, производитель) лист выпускается как «Спецификация светильников».
3. Длина LED-ленты в карнизе — по линии карниза плана потолков (лист 36); Σ P = Вт/м × длина. Блок питания загружен не больше чем на 80 %; лента 24 В длиннее 10 м питается с двух концов; доступ к блоку питания — люк ревизии 300×300 мм или место, указанное в таблице.
4. Сценарии: % — яркость группы на светорегуляторе; «вкл.» — группа на обычной клавише; группы, не названные в строке, выключены. Светильники и блоки питания групп на светорегуляторе — с регулировкой яркости. Клавиши и светорегуляторы — лист 47.
5. Мощность и поток в таблице — требования к подбору (поток не меньше, мощность не больше указанных); после выбора модели — по её паспорту, Σ P — установленная мощность освещения. Оценка освещённости — на плане освещения; это не светотехнический расчёт.

					Проект: Четырёхкомнатная квартира
	Лист	№ док.	Подпись	Дата	
Дизайнер	Кырлан А.С.			04.11.26	Техническое задание на подбор светильников
					Стадия: П; Лист: 46; Листов: 120

Условные обозначения

- ⊕ — светильник подвесной
- L1 — группа включения у светильника
- светильник настенный (бра), H — высота оси
- стояк: К1 — канализация, В1 — ХВС, Т3 — ГВС
- светодиодная лента в профиле / в карнизе короба
- (1) — номер помещения, площадь м²

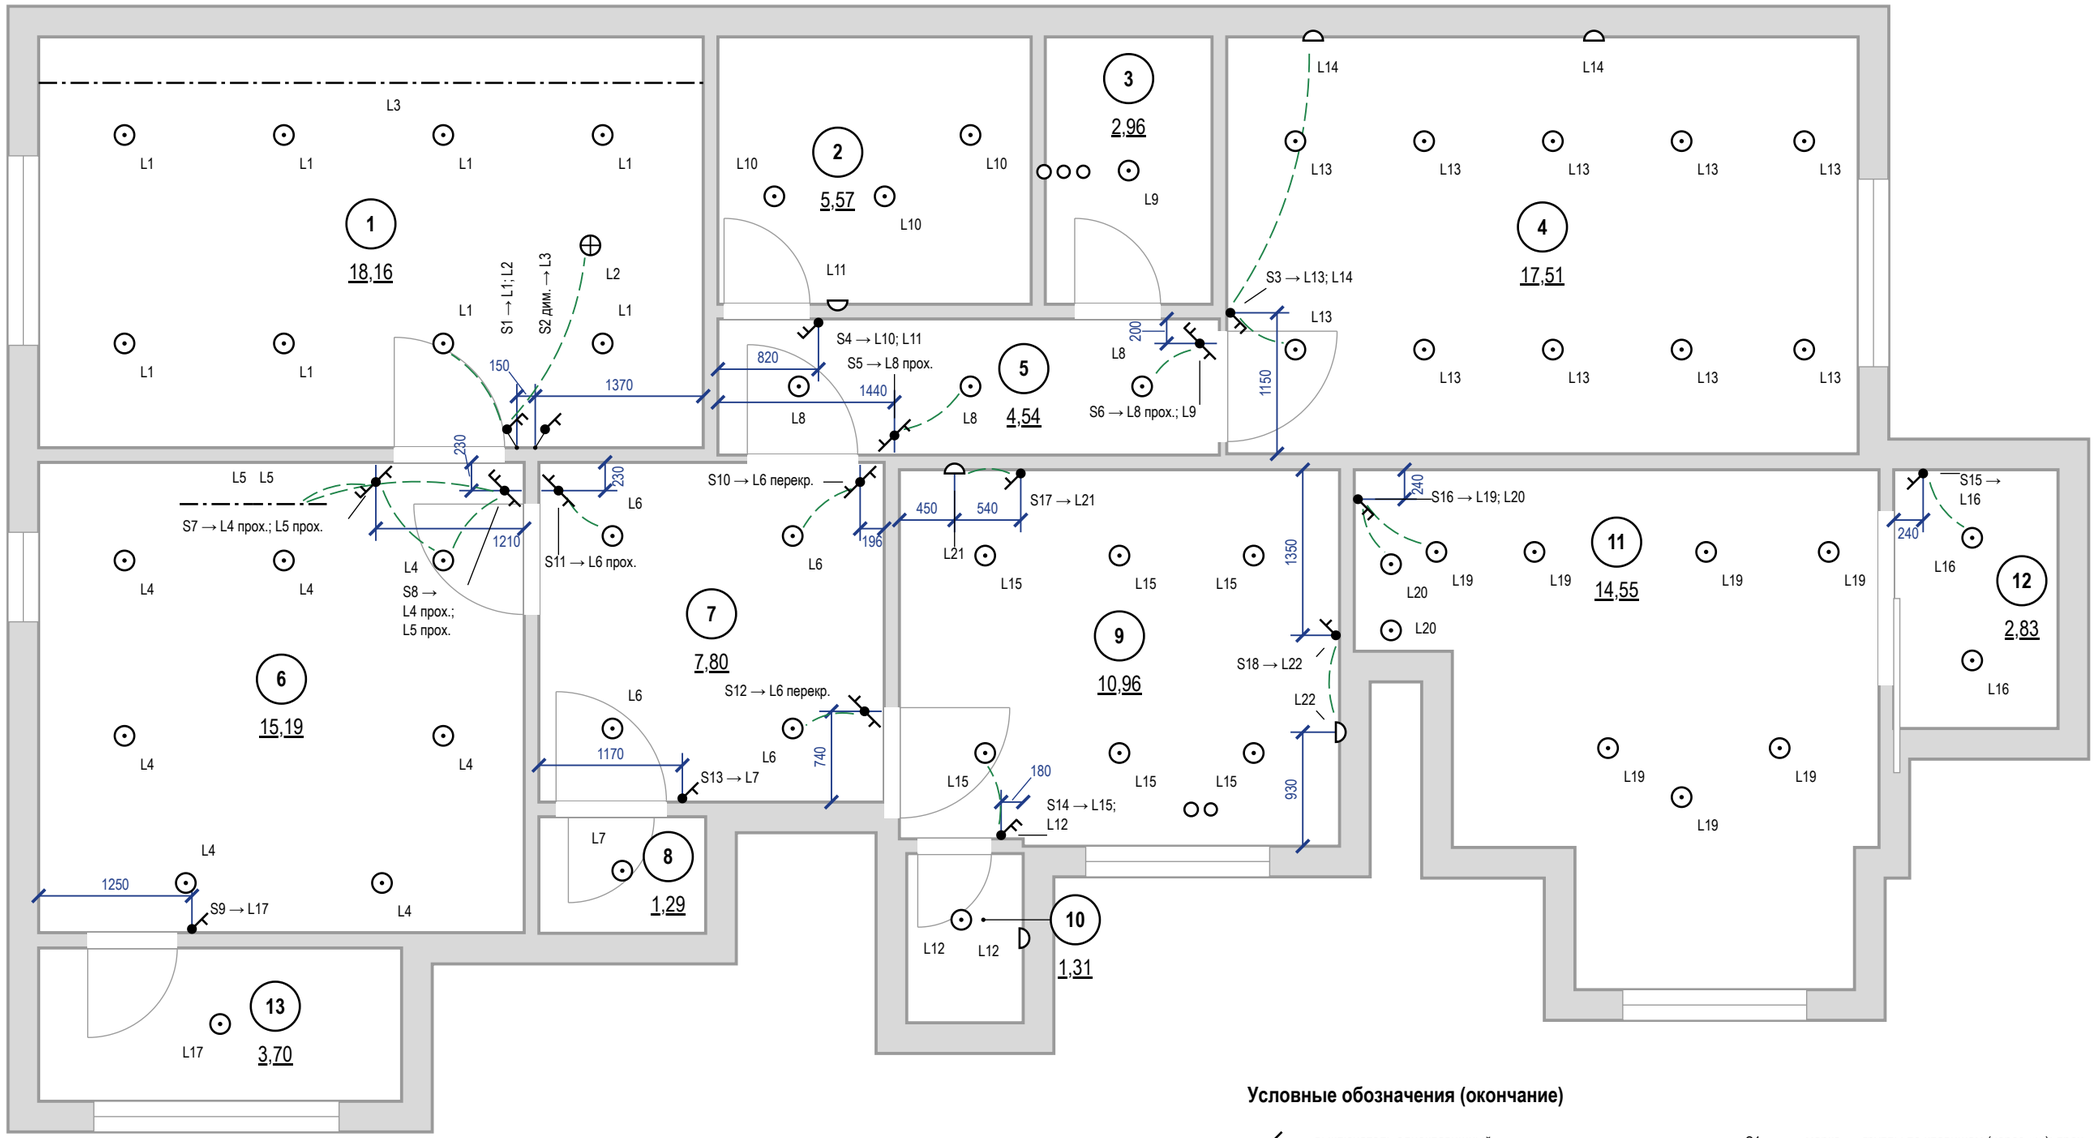


Примечания

1. За отметку 0,000 принят уровень чистого пола. Высоты H — от чистого пола до оси изделия; привязки — от чистовой грани стены до оси механизма (у рамки на несколько постов — до оси рамки).
2. Высота установки, не указанная на плане: выключатели — 900 мм от чистого пола (у кровати и другие — H у марки), со стороны дверной ручки (ПУЭ 7.1.51).
3. Какой выключатель какие светильники включает — по номеру группы L: у выключателя (S1 → L1; L2 — клавиши по порядку) и у каждого светильника. Пунктир подсказка к ближайшему светильнику группы в том же помещении (не дальше 3 м), это не трасса кабеля; выключатель за стеной (у двери санузла) и далёкая группа — только номер группы.
4. Группы из нескольких мест (L8 — S5, S6; L4 — S7, S8; L5 — S7, S8; L6 — S10, S11, S12): на крайних местах — проходные клавиши, на промежуточных перекрёстные; механизмы — в ведомости изделий.
5. Светорегулятор — по заднему фронту (для LED-драйверов), совместимость с драйверами проверить до закупки.
6. Розеточные и мокрые линии — через УЗО или дифавтомат с током утечки не более 30 мА (ПУЭ 7.1.79); в санузле выполнить ДСУП (ПУЭ 7.1.87–7.1.88).
7. Кабель — медный, исполнение нг(А)-LS (ГОСТ 31565-2012); скрытая прокладка только горизонтально и вертикально, фактические трассы зафиксировать исполнительной схемой до закрытия отделкой.
8. Расчёт нагрузок, токов КЗ, селективности и сечений — по проекту ЭОМ организации с допуском СРО; лист задаёт состав, расположение и группы.

Условные обозначения (окончание)

- выключатель одноклавишный
- выключатель двухклавишный (флажков — по числу клавиш)
- выключатель с проходной или перекрёстной клавишей (обратный флажок); тип клавиши — в подписи
- S1 → — марка → группы по клавишам (через «;»): прох. проходной, перекр. — перекрёстный, дим. светорегулятор; H — высота
- связь: выключатель → ближайший светильник группы в том же помещении (не трасса кабеля); полный состав группы по номеру L
- светильник встраиваемый точечный

					Проект: Четырёхкомнатная квартира — М 1:50
	Лист	№ док.	Подпись	Дата	Управление светильниками — Стадия: П; Лист: 47; Листов: 120
Дизайнер	Кырлан А.С.			04.11.26	

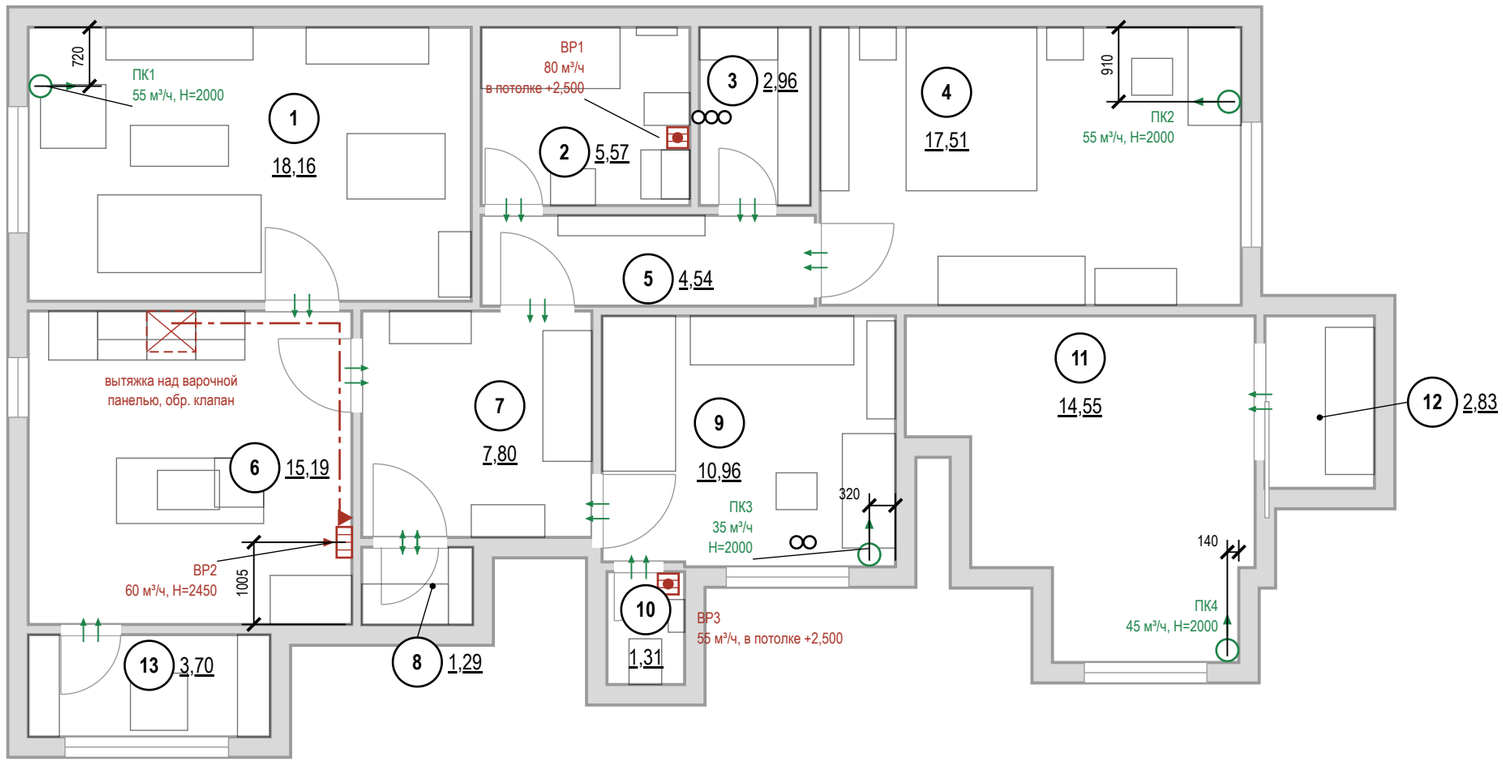

Условные обозначения

- стояк: К1 — канализация, В1 — ХВС, Т3 — ГВС
- номер помещения, площадь м²
- вытяжная решётка в вентканал: марка, расход м³/ч, Н центра от чистого пола
- вентилятор с обратным клапаном в подшивном потолке, воздуховод за потолком до канала
- приточный клапан (КИВ) в наружной стене: марка, расход, Н центра
- переток: зазор под полотном или переточная решётка
- кухонная вытяжка над варочной панелью
- воздуховод кухонной вытяжки в коробе под потолком
- отдельный вход воздуховода в вентканал, обратный клапан

Воздухообмен, м³/ч

№	Помещение	Выт. норма	Выт. проект	Прит. норма	Прит. проект	Устрой-ства
1	Зал			55	55	ПК1
2	Ванная комната	50	80			ВР1
3	Тёмная комната	2				переток
4	Детская 1			53	55	ПК2
6	Кухня	60	60			ВР2
8	Гардеробная 2	1				переток
9	Детская 2			33	35	ПК3
10	Санузел	25	55			ВР3
11	Гостиная			44	45	ПК4
12	Гардеробная 1	2				переток
	Итого	**140**	**195**	**185**	**190**	

Воздухообмен квартиры — по большей из сумм притока и вытяжки: норма 185 м³/ч, проект 195 м³/ч.
Вытяжка не меньше притока — баланс сведён.

Привязки — до обмера
Вентканалы в исходных данных не заданы: решётки и вход вытяжки показаны у стояков К1 (вентблок у мокрой зоны). До черновых работ — обмер каналов и проверка тяги; лист перевыпустить по факту.

Примечания


1. Расчёт систем ОВ и подбор оборудования — проектная организация с допуском СРО; лист даёт места, трассы и привязки.
2. Нормы вытяжки — СП 54.13330.2022 (Изм. 1, 2), табл. 7.1: кухня с электроплитой 60 м³/ч, с газовой 100; ванная и совмещённый санузел 50; уборная 25; гардеробная 0,2 ч⁻¹. Приток в жилые — 3 м³/ч на 1 м² (менее 20 м² общей площади на человека), иначе 30 м³/ч на человека.
3. Вентканалы и шахты не сужать, не переносить и не закрывать; вентилятор и кухонная вытяжка — через обратный клапан, без перекрытия естественной тяги.
4. Проектные расходы — не ниже нормы, вытяжка сведена с притоком вентиляторами мокрых помещений. Клапаны — в простенке у окна, центр 2000 мм, не над кроватью, не ближе 300 мм к стоякам отопления; типоразмер — на расход.
5. Под подшивным потолком вытяжка — в потолке, воздуховодом за потолком до канала. Кухонная вытяжка в воздухообмен не включена: воздуховод не менее Ø125 в коробе, вход в канал отдельный.
6. Переток — зазор под полотнами межкомнатных дверей или переточная решётка.
7. Кондиционирование заданием не предусмотрено; при установке трассы фреона и дренажа (не менее 40 мм/м, в К1 через сифон) и питание заложить до черновых работ.
8. Привязки оборудования — по паспортам приобретённых моделей, до черновых работ.

					Проект: Четырёхкомнатная квартира — **М 1:75**
	Лист	№ док.	Подпись	Дата	
Дизайнер	Кырлан А.С.			04.11.26	План вентиляции

Стадия	Лист	Листов
П	48	120

Условные обозначения

- (1) — номер помещения, площадь м²
- радиатор отопления (марка РО-N, длина по плану)
- (Т) — клапан с термоголовкой на подаче
- стояк отопления, подающий (Ст Т1-N)
- стояк отопления, обратный (Ст Т2-N)
- Т1 — отопление, подающий трубопровод
- Т2 — отопление, обратный трубопровод

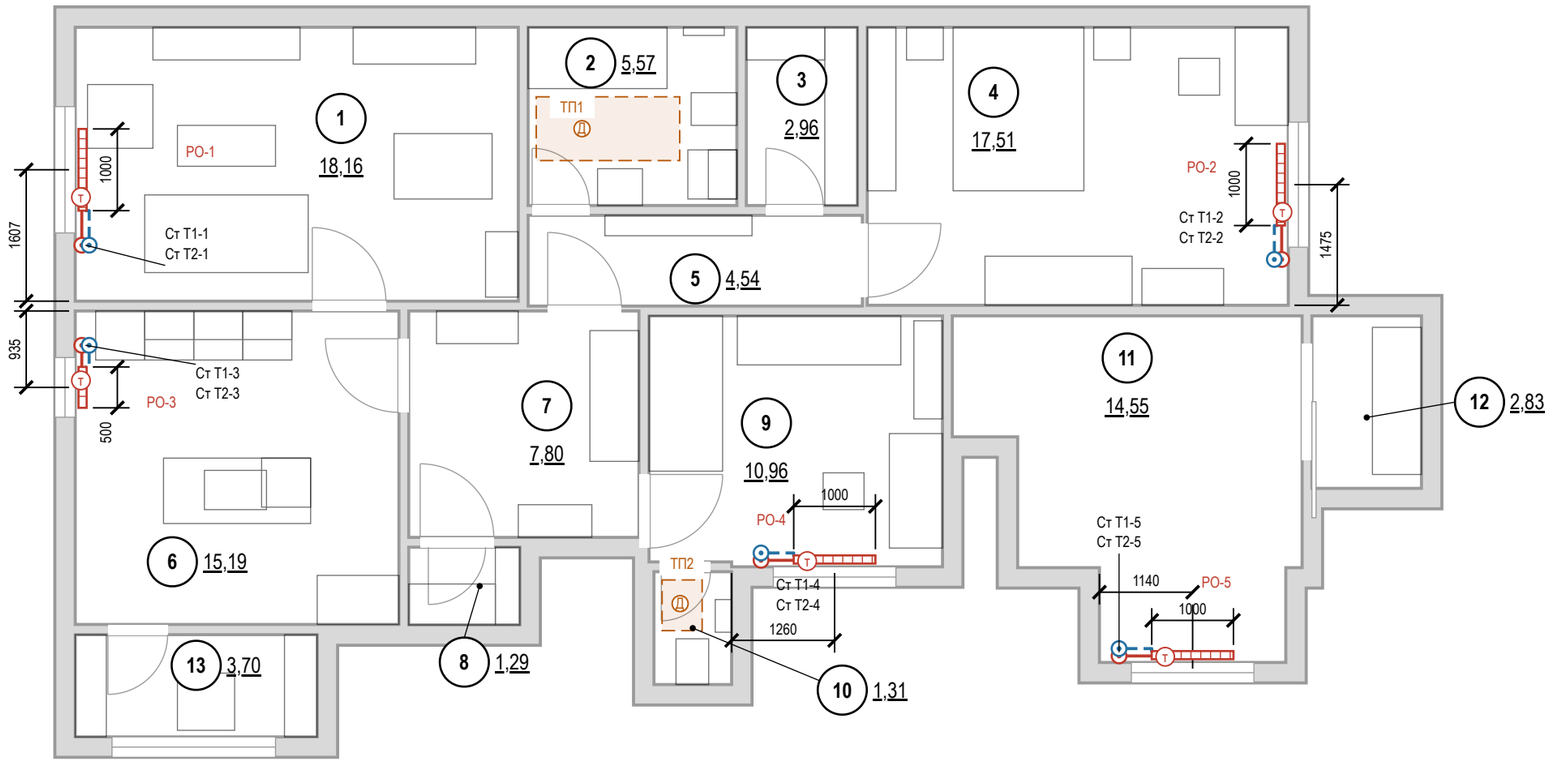

Ведомость радиаторов

Марка	Помещение	Тип	Д×В×Г, мм	Низ / стена	Q, Вт
РО-1	1. Зал	панельный	1000×500×100	120 / 40	расч.
РО-2	4. Детская 1	панельный	1000×500×100	120 / 40	расч.
РО-3	6. Кухня	панельный	500×500×100	120 / 40	расч.
РО-4	9. Детская 2	панельный	1000×500×100	120 / 40	расч.
РО-5	11. Гостиная	панельный	1000×600×100	120 / 40	расч.

тип и мощность — по теплотехническому расчёту
Низ — от чистого пола, стена — зазор до задней панели, мм.

Привязки — до обмера
Стояки отопления в исходных данных не заданы: показаны у откосов окон, подводки — принципиально. До черновых работ — обмер стояков и паспорта приборов; лист перевыпустить по факту.

Примечания

1. Расчёт системы отопления, теплопотерь и подбор приборов — проектная организация с допуском СРО; лист даёт места и привязки.
2. Электрический тёплый пол: ТП1 — пом. 2, мат 1755×780 мм, 205 Вт; ТП2 — пом. 10, мат 490×620 мм, 50 Вт; контуры показаны пунктиром; датчик температуры (Д) — в гофротрубе, трасса к терморегулятору — по обмеру. Марка мата и точное положение датчика — при закупке и по обмеру.
3. Тип, длина и мощность радиаторов — по теплотехническому расчёту; лист задаёт места, зазоры и подключение.
4. Радиаторы — под каждым окном жилых комнат и кухни, центр по оси проёма, длина 0,7 ширины окна (кратно 100); окончательно — по расчёту.
5. Зазоры радиатора: низ не менее 100 мм от чистого пола, верх не менее 100 мм до подоконника, 30–50 мм от стены до задней панели; центр по оси окна с допуском ±20 мм. Верх до подоконника — 180 мм.
6. Радиаторы не закрывать глухими коробами и мебелью; перенос и замена приборов в многоквартирном доме — переустройство, согласование с управляющей организацией (ЖК РФ ст. 25–26); вынос на лоджию запрещён.
7. Трубы отопления через межквартирные стены не прокладывать (СП 51.13330.2011, п. 9.19); через перекрытия и перегородки — в гильзах.
8. Привязки приборов и подводок — по паспортам приобретённых радиаторов и клапанов, до черновых работ.
9. До закрытия отделкой трубопроводы отопления испытать гидростатическим давлением с оформлением акта (СП 73.13330.2016, 7.2–7.3).

					Проект: Четырёхкомнатная квартира — **М 1:75**
	Лист	№ док.	Подпись	Дата	
Дизайнер	Кырлан А.С.			04.11.26	План отопления

Стадия	Лист	Листов
П	49	120


выпуск 04.11.2026 № 2391fcbada · стр. 49 из 120

Спецификация плинтусов

Наименование	Помещения	Длина, м (с запасом)
Плинтус МДФ под окраску 80×16 мм, крепление к стене, окраска в цвет Tikkurila F497	1, 3, 4, 6, 8, 9, 11, 12	99
Плинтус МДФ под окраску 80×16 мм, крепление к стене, окраска в цвет Tikkurila J484	5, 7	19
Плинтус из керамогранита пола, подрезка 80 мм, верхняя кромка с запилом 45°, h = 80 мм, крепление к стене	13	9

Отметки по высоте

±0,000	чистый пол пом. 1, 3–9, 11, 12; отсчёт высот
−0,015	чистый пол пом. 2, 10, ниже на 15 мм
−0,030	чистый пол пом. 13, ниже на 30 мм
−0,170	верх плиты — расчёт, не замер (задание на обмер)
сущ. пол	снимается до плиты; не замерен (задание на обмер)

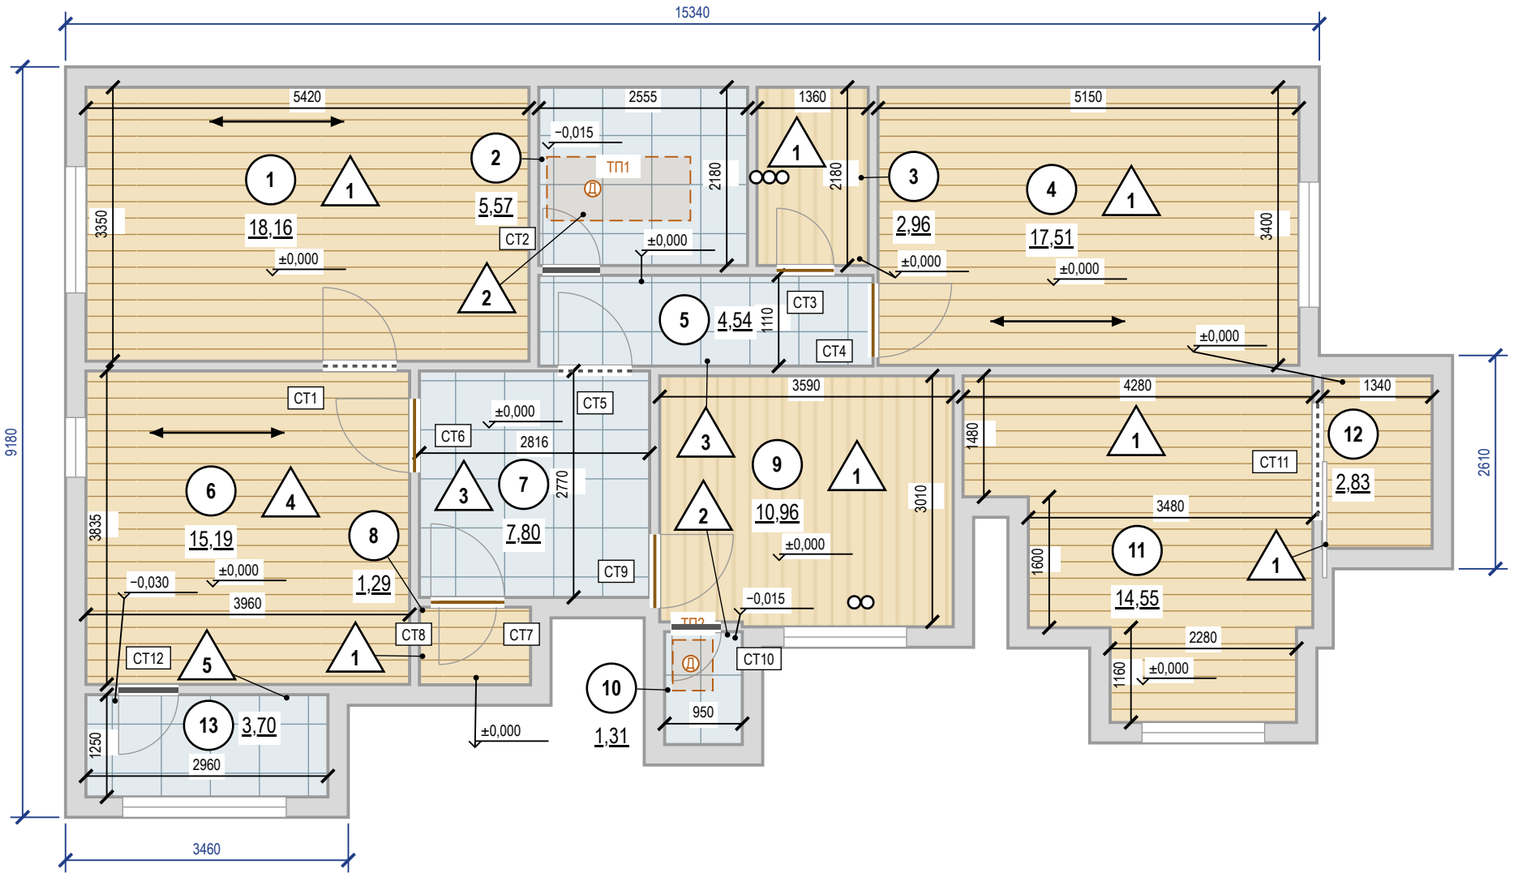

Экспликация полов


Номер помещения	Тип пола	Схема пола	Данные элементов пола (наименование, толщина, основание), мм	Площадь, м²
1, 3, 4, 8, 9, 11, 12	1		Инженерная доска дуб на клею — 14 Клей паркетный МС-полимерный — 1 Стяжка ЦПС М300 (В22,5), фибра, по звукоизоляции — 55 Звукоизоляция — минплита 110 кг/м³ 20 Засыпка керамзитовая фр. 0–5, уплотнённая — 80 Плита перекрытия монолитная Всего 170 мм; ЧП ±0,000, верх плиты −0,170	68,26
2, 10	2		Керамогранит 600×600×10 — 10 Нагревательный мат в слое клея С2 TE S1 — 8 Гидроизоляция обмазочная, 2 слоя (заход на стены — по ведомости отделки) — 2 Сборное основание ГВЛВ 2×12,5 — 25 Засыпка керамзитовая сухая фр. 0–5 (в слое — выпуски К1) — 110 Плита перекрытия монолитная Всего 155 мм; ЧП −0,015, верх плиты −0,170	6,88
5, 7	3		Керамогранит 600×600×10 — 10 Клей плиточный С2 TE S1 — 5 Стяжка ЦПС М300 (В22,5), фибра, по звукоизоляции — 55 Звукоизоляция — минплита 110 кг/м³ 20 Засыпка керамзитовая фр. 0–5, уплотнённая — 80 Плита перекрытия монолитная Всего 170 мм; ЧП ±0,000, верх плиты −0,170	12,34
6	4		Инженерная доска дуб на клею — 14 Клей паркетный МС-полимерный — 1 Гидроизоляция полиуретановая, 2 слоя (зона мойки и острова) — 2 Стяжка ЦПС М300 (В22,5), фибра, по звукоизоляции — 53 Звукоизоляция — минплита 110 кг/м³ 20 Засыпка керамзитовая фр. 0–5, уплотнённая — 80 Плита перекрытия монолитная Всего 170 мм; ЧП ±0,000, верх плиты −0,170	15,19
13	5		Керамогранит 600×600×10 — 10 Клей плиточный С2 TE S1 (деформируемый) — 5 Сборное основание ГВЛВ 2×12,5 — 25 Пенополистирол экструзионный 2×50 100 Плита перекрытия монолитная Всего 140 мм; ЧП −0,030, верх плиты −0,170	3,70
			Итого	**106,37**

Примечания


1. За отметку ±0,000 принят чистый пол, не существующий (блок отметок). Площади — по чистым размерам помещений, м²; размеры — в мм.
2. Стык разнотипных покрытий — по оси дверного полотна (под полотном в закрытом положении); решение стыка — по ведомости стыков.
3. Размеры помещений в свету (ширина × длина, мм), не поместившиеся на плане: пом. 5 — 4090 × 1110; пом. 8 — 1360 × 950; пом. 9 — 3590 × 3010, 2580 × 60; пом. 10 — 950 × 1380; пом. 12 — 1340 × 2110.
4. Пол санузлов ниже смежных помещений на 15 мм за счёт меньшей толщины стяжки (верх плиты общий — по экспликации полов); гидроизоляция по стяжке с заведением на стены не менее 200 мм (СП 29.13330.2011, п. 7.2), до облицовки — тест проливом и акт скрытых работ.
5. Выпуски канализации с уклоном и трассы водоснабжения — в слое засыпки под стяжкой (по экспликации полов); отметки, уклоны и прочистки — по листу разводки ВК 23.
6. Штучные покрытия (инженерная доска): направление — по стрелке; влажность основания по СМ не более 2,0 % (по ТУ изготовителя).
7. Ровность основания — просвет под 2-метровой рейкой не более 2 мм: пом. 1, 3, 4, 6, 8, 9, 11, 12 (инженерная доска), пом. 2, 5, 7, 10 (керамогранит); 3 мм: пом. 13 (керамогранит); проверить до укладки покрытия (СП 71.13330.2017, табл. 8.5).
8. Плавающая стяжка по звукоизоляции: демпферная (кромочная) лента по контуру помещения, у стояков и колонн — до верха чистого пола (СП 51.13330.2011, п. 9.11); плинтус крепится только к стене.
9. Сетка на плитке — условная, в размер формата; точка старта и раскладка — по листу раскладки плитки.
10. Узор покрытия (заливка-код типа пола) прерывается под надписями — площадями помещений и отметками чистого пола.
11. Электрический тёплый пол: ТП1 — пом. 2, мат 1755×780 мм, 205 Вт; ТП2 — пом. 10, мат 490×620 мм, 50 Вт; контуры показаны пунктиром; датчик температуры (Д) — в гофротрубе, трасса к терморегулятору — по обмеру. Марка мата и точное положение датчика — при закупке и по обмеру.
12. Пироги полов — по экспликации полов: слои сверху вниз, толщины в мм; гидроизоляция мокрых зон — в пироге и в ведомости отделки; схема пола — без масштаба.

					Проект: Четырёхкомнатная квартира — **М 1:75**
	Лист	№ док.	Подпись	Дата	План покрытий пола
Дизайнер	Кырлан А.С.			04.11.26	Стадия: П; Лист: 50; Листов: 120


Фрагмент 1. Ванная комната (пом. 2). Пол 600×600, шов 2 мм, М 1:50

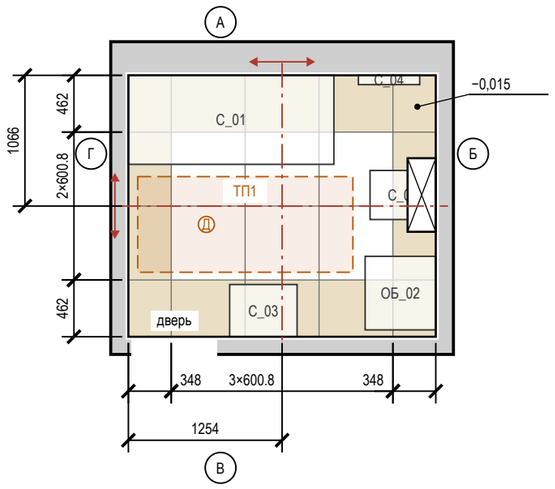


Фрагмент 2. Коридор (пом. 5). Пол 600×600, шов 2 мм, М 1:50

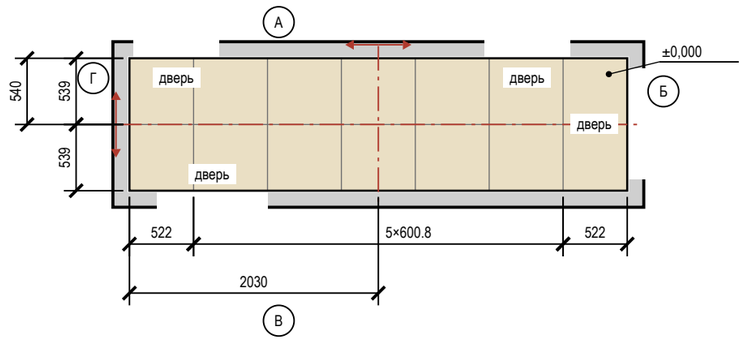

Фрагмент 3. Прихожая-коридор (пом. 7). Пол 600×600, шов 2 мм, М 1:50

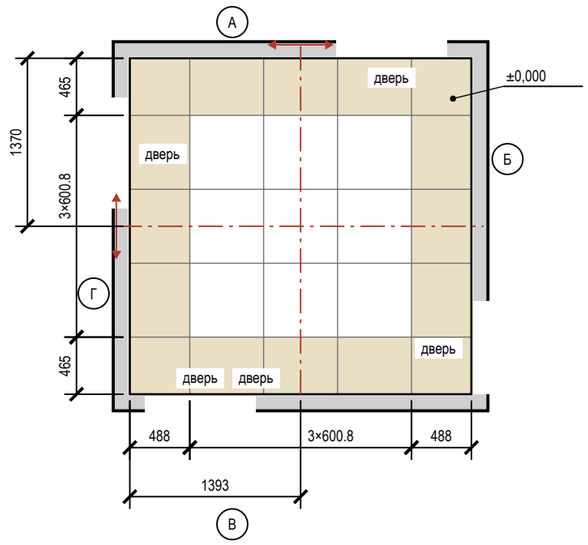

Фрагмент 4. Санузел (пом. 10). Пол 600×600, шов 2 мм, М 1:50

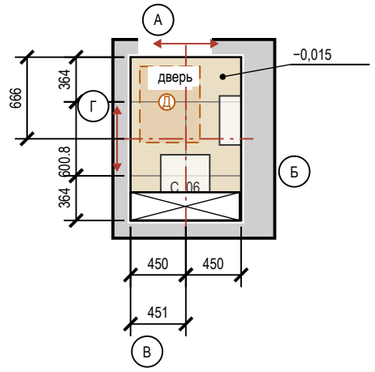

Ведомость материалов

Материал	Класс, код	Норма расхода	Кол-во
Затирка	CG2WA аналог: Mapei Ultracolor 133	(a+b)/ab·шов·t·1,6	5,6 кг
Затирка	CG2WA	(a+b)/ab·шов·t·1,6	0,1 кг
Клей	C2 TE S1 аналог: Litokol K80 Eco	1,5 кг/м²·мм, слой 5	425 кг (17 меш.)
Клей	C2 TE S1	1,5 кг/м²·мм, слой 5	10 кг (1 меш.)
Гидроизоляция	обмазочная, 2 слоя: пол, стены по периметру и зоны замачивания	по ТУ	16,2 м²
Демпф. лента	по периметру пола из плитки		29,1 м

Ведомость плитки

Помещение, поверхность	Плитка, код	Формат	Шов	S, м²	Целых	Подр.	С запасом
Ванная комната, пол	керамогранит матовый R10, тон J484	600.8×600.8	2	5,57	6	14	22
Ванная комната, стены А–Г	керамогранит матовый, тон F497	600.8×600.8	2	21,66	23	67	100
Ванная комната, короб инсталляции	керамогранит матовый, тон F497	600.8×600.8	2	1,36	1	6	8
Коридор, пол	керамогранит матовый R10, тон V486	600.8×600.8	2	4,54	0	14	16
Прихожая-коридор, пол	керамогранит матовый R10, тон V486	600.8×600.8	2	7,80	9	16	28
Санузел, пол	керамогранит матовый R10, тон J484	600.8×600.8	2	1,31	0	6	7
Санузел, стены А–Г	керамогранит матовый, тон F497	600.8×600.8	2	9,44	6	44	56
Санузел, короб инсталляции	керамогранит матовый, тон F497	600.8×600.8	2	1,76	0	10	11
Кухня, фартук (ст. А)	аналог: керамогранит матовый, тон F497	600.8×600.8	2	1,11	1	3	5
Итого 600.8×600.8				**54,54**	**46**	**180**	**253**

Условные обозначения


- плитка целая; тонкая линия — шов
- плитка с подрезкой (размер — на цепочке)
- ось старта; стрелки — направление укладки
- сантехприбор: габарит, высота по практике
- короб инсталляции: плитка пола — до короба
- электрический тёплый пол: контур мата ТП, Д — датчик
- отметка чистого пола на полке выноски, м
- А — обозначение стены А–Г (как на развёртках)

Примечания

1. Раскладка от чистовых размеров: стены санузлов теряют 10 + 5 + 9 = 24 мм на сторону (штукатурка, клей, плитка); подрезки — чистые, без шва.
2. Старт — от центра помещения (штрихпунктир, стрелки — направление укладки); размер старта — от чистовых стен Г и А.
3. Раскладка фартука «Кухня» — на листе «Раскладка плитки. Фартук кухни».
4. Количество: целые по раскладке + по одной на подрезку, запас 10 %; один артикул — одна партия и тон. Исключены поддон, короб, проёмы и места за коробом; S — по чистым граням: стены нетто = зона облицовки по ведомости отделки − место за коробом инсталляции 1,71 м² (плитку за коробом не кладут), короб — отдельной строкой.
5. Клей C2 TE S1 аналог: Litokol K80 Eco; C2 TE S1 (ГОСТ Р 56387-2018), затирка CG2WA аналог: Mapei Ultracolor 133; CG2WA; расход — по ТУ выбранной марки.
6. Гидроизоляция: пол и стены 200 мм от ЧП; над ванной — до 2100 и 300 мм за борт (пом. 2) (см. развёртки); акт скрытых работ, пролив 24 ч.
7. Электрический тёплый пол: ТП1 — пом. 2, мат 1755×780 мм, 205 Вт; ТП2 — пом. 10, мат 490×620 мм, 50 Вт; контуры показаны пунктиром; датчик температуры (Д) — в гофротрубе, трасса к терморегулятору — по обмеру. Марка мата и точное положение датчика — при закупке и по обмеру. Плитку над матом клеить клеем, который изготовитель допускает для тёплого пола, до включения выдержать срок по ТУ клея.
8. Швы пола совмещены со швами стены А; по периметру — демпферная лента.
9. Отметка чистого пола −0,015, порог 15 мм; стык с соседним покрытием — по оси полотна двери.

					Проект: Четырёхкомнатная квартира	М 1:50
	Лист	№ док.	Подпись	Дата	Раскладка плитки. Планы полов	Стадия: П; Лист: 51; Листов: 120
Дизайнер	Кырлан А.С.			04.11.26		

Фрагмент 1. Кухня (пом. 6), фартук, стена А. 600×600, шов 2 мм, М 1:20

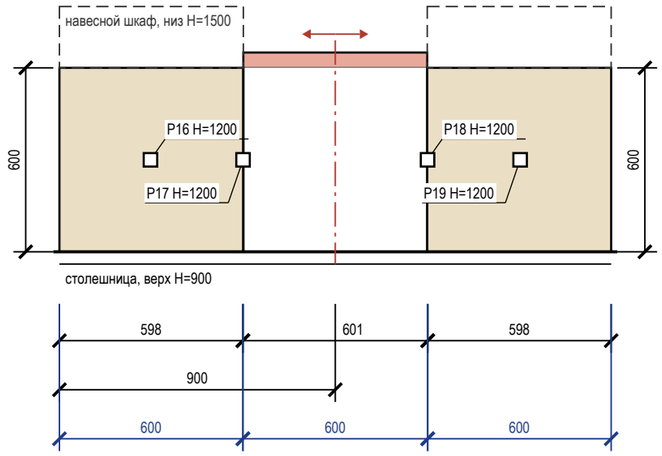

Условные обозначения

- плитка целая; тонкая линия — шов
- плитка с подрезкой (размер — на цепочке)
- ось старта; стрелки — направление укладки
- электроточка: марка и Н — по листам ЭОМ
- столешница (верх)
- навесной шкаф над фартуком

Подсчёт плитки

Поверхность	Формат	S, м²	Целых	Подр.	С запасом
Кухня, фартук (ст. А)	600×600	1,11	1	3	5

Примечания

1. Фартук, Кухня: 600×600 горизонтально, шов 2 мм; зоны 600 мм — 900…1500, 600 мм — 900…1550, 600 мм — 900…1500 (от столешницы до низа навесного шкафа, без шкафа — 650 мм). Старт от центра участка, подрезки 598 мм. Площадь 1,11 м² — как в ведомости отделки.
2. Фартук — после монтажа столешницы, низ на 2–3 мм выше неё, шов со столешницей — санитарный герметик; навесные шкафы — после фартука. Торцы у пенала и стены — профиль или запил 45°.
3. Фартук, Кухня: в зоне до отм. 1550 верхний ряд подрезан 47 мм — меньше 1/3 плитки; полоса прикрыта корпусом навесного модуля и на виду не остаётся. Раскладкой не снимается: убрать подрезку можно, только выровняв низ этого модуля с соседними (1500 мм) — решение мебельщика.
4. Клей, затирка и итог по форматам — в ведомостях листа «Раскладка плитки. Планы полов».

					Проект: Четырёхкомнатная квартира	М 1:20
	Лист	№ док.	Подпись	Дата	Раскладка плитки. Фартук кухни	Стадия / Лист / Листов
Дизайнер	Кырлан А.С.			04.11.26		П / 52 / 120

Развёртка стены А


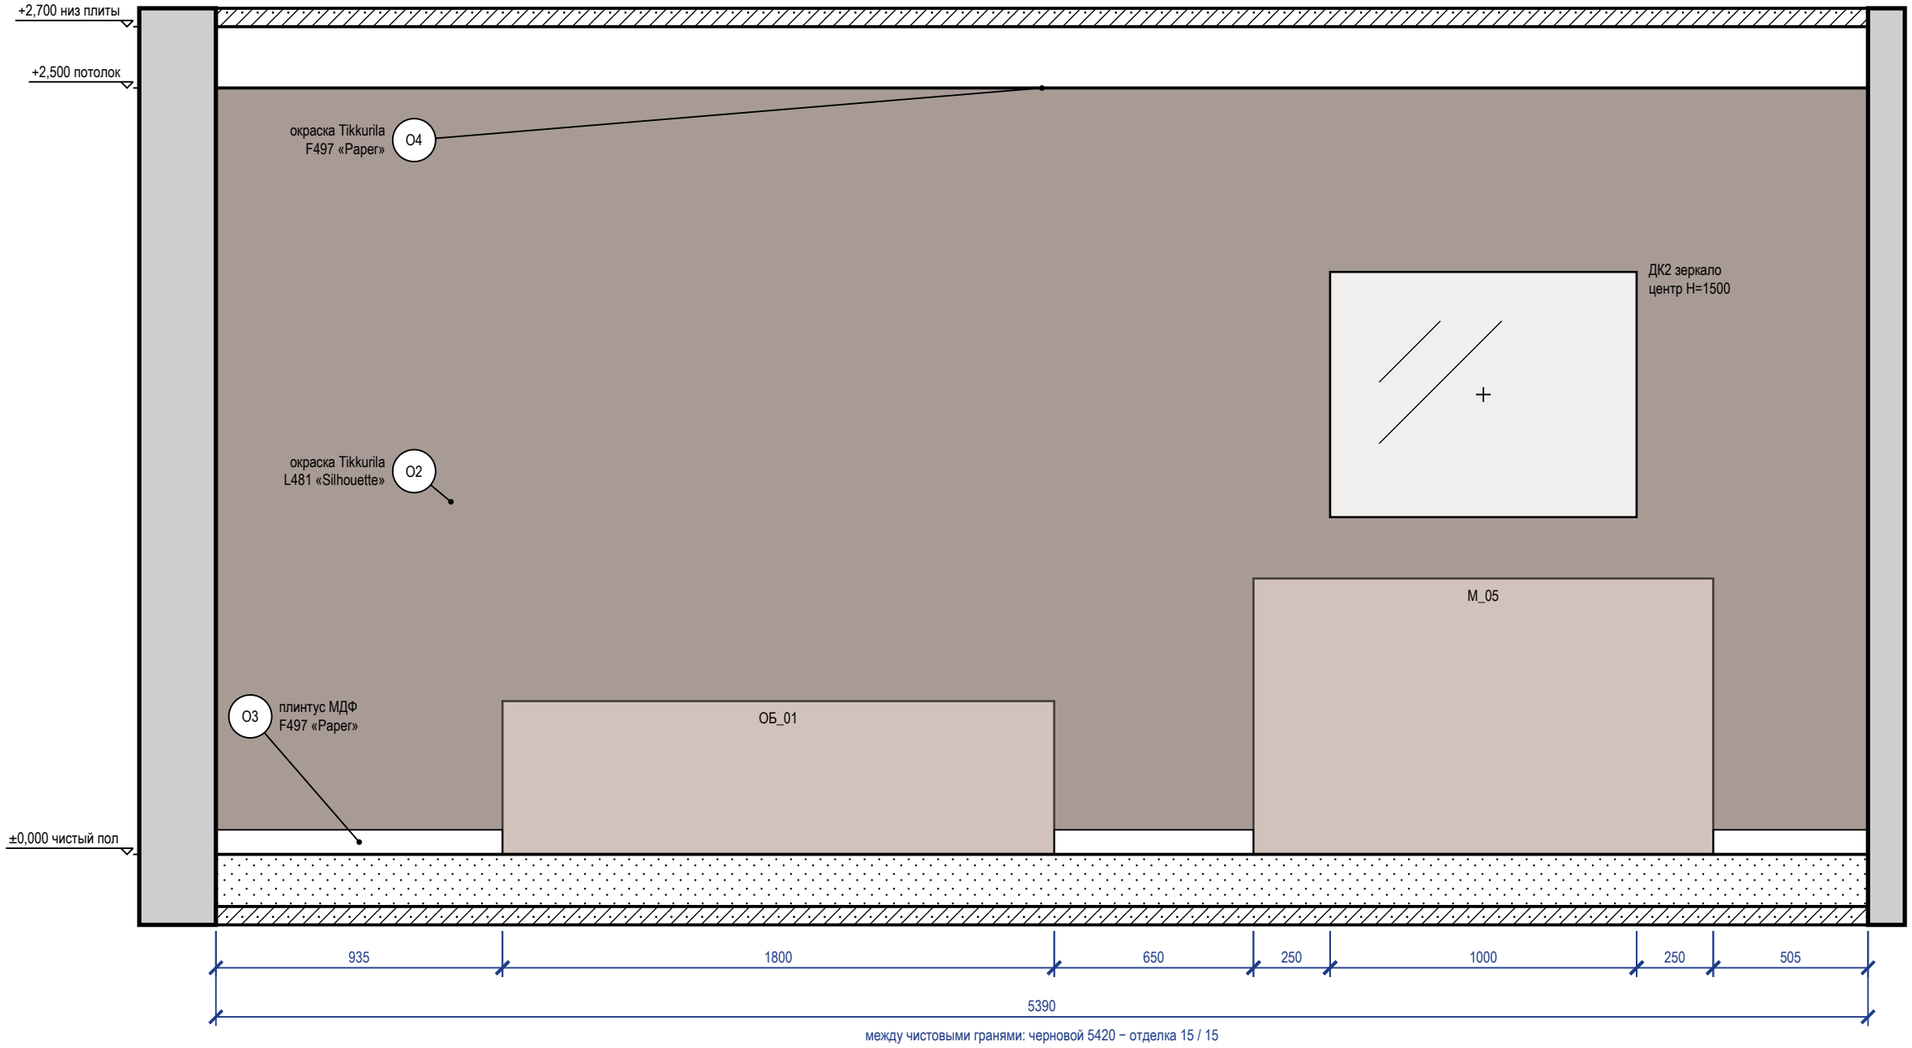


Схема развёрток (М 1:100)

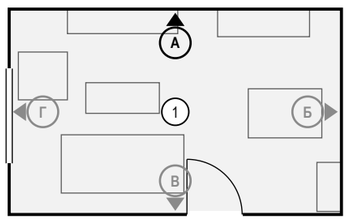

Ведомость отделки (на листе)

Марка	Поверхность	Материал, изделие	Цвет, код	Кол.
О2	акцентная стена	окраска, Tikkurila Optiva 5 Matt, аналог: интерьерная краска, класс 2 по EN 13300, глубокоматовая/матовая, база С, матовая, подготовка К3	Tikkurila L481 «Silhouette»	13,5 м²
О3	плинтус	плинтус МДФ, h 80 мм, аналог: плинтус МДФ под окраску 80×16 мм, полуглянцевая	Tikkurila F497 «Paper»	2,1 м
О4	потолок	окраска, Tikkurila Anti-Reflex 2, глубокоматовая, подготовка Q3	Tikkurila F497 «Paper»	18,2 м²

Примечания

1. Размеры — в мм от чистовых поверхностей стен; условные обозначения и общие указания — лист 3.
2. Стена А показана двумя видами: здесь — архитектурная развёртка (мебель, отделка, проёмы, высоты), электроточки и выводы ВК с привязками и таблицей — на листе 54 («Привязки»).
3. Картины и зеркала крепить к основанию по паспорту изделия (закладные и анкеры — в перечне скрытых работ); крест — ось центра предмета.
4. Потолок — у каждой стены свой, по плану потолков (ПТ1); ступени — зоной, кромка короба перед нишей — тонкой линией; в поле потолка: ПТ2 +2,600.

	Лист	№ док.	Подпись	Дата
Дизайнер	Кырлан А.С.			04.11.26

Проект: Четырёхкомнатная квартира — М 1:20

Развёртка стены А. Зал (пом. 1)

Стадия	Лист	Листов
П	53	120

Развёртка стены А: электроточки и выводы

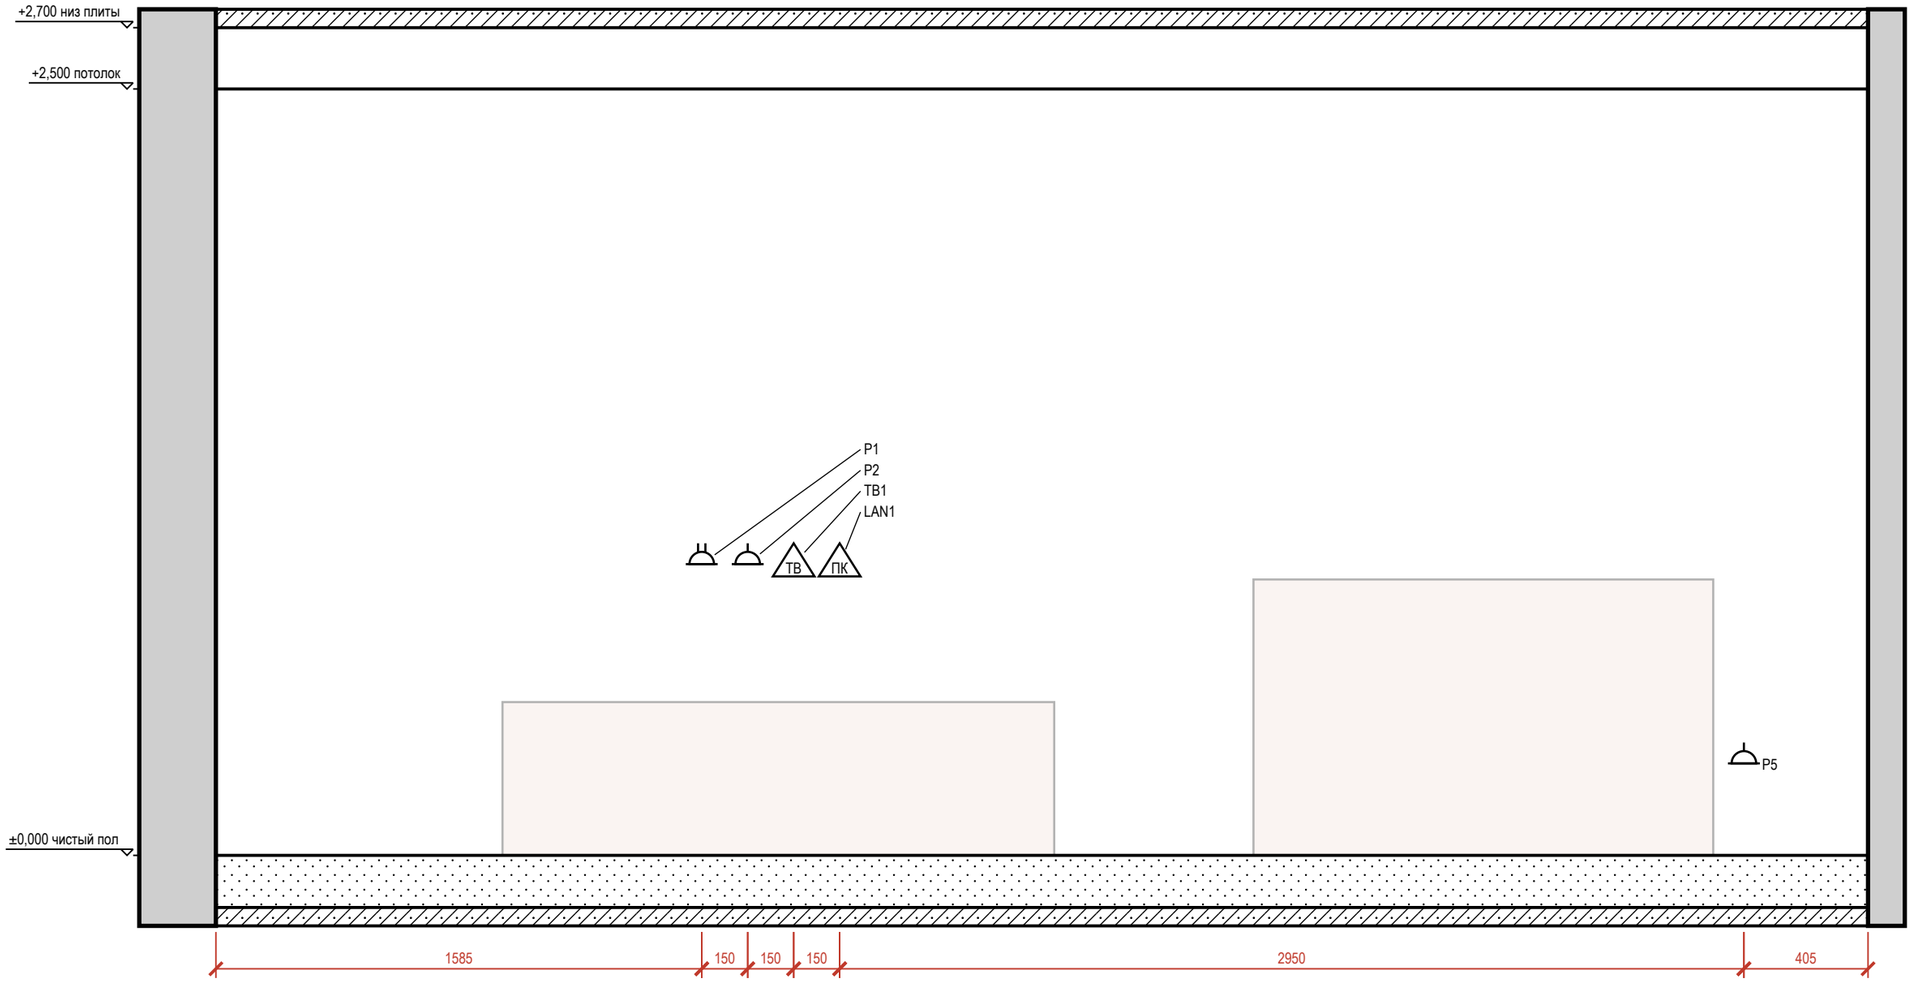



Таблица привязок электроточек и выводов

Марка	Назначение	От угла, мм	Н от пола, мм	Примечание
P1	розетка: ТВ-зона: телевизор, медиаплеер	1585	950	рамка 2 поста, гр. 5
P2	розетка: ТВ-зона: саундбар	1735	950	гр. 5
TB1	розетка ТВ: ТВ-зона	1885	950	
LAN1	розетка RJ45: ТВ-зона	2035	950	
P5	розетка: обеденная зона, буфет M_05	4985	300	гр. 5

Условные обозначения

- розетка с заземляющим контактом; у знака — марка, ×N постов в рамке, гр. — группа щита, Н — высота оси, мм
- ПК — розетка компьютерная RJ45
- ТВ — розетка телевизионная
- привязки точек и выводов от угла и от пола, мм
- А — марка развёртки: буква стены, стрелка — взгляд

Схема развёрток (М 1:100)

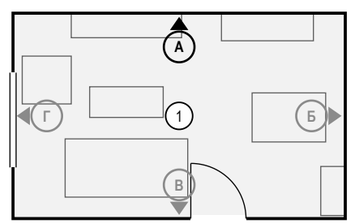

Примечания

1. Вид «Привязки» стены А — электроточки и выводы ВК; архитектурная развёртка (мебель, отделка, проёмы, высоты) — на листе 53. Мебель и приборы — подложкой для ориентира; их марки и обозначения мебели, проёмов и стен — там же.
2. Привязки — в мм: по горизонтали от левого чистового угла стены до оси изделия, Н — от чистого пола до оси; все точки — в таблице привязок. Красная цепочка — привязки по осям; точки ближе 120 мм одна к другой в цепочку не дробятся — их привязки только в таблице.
3. У знака — марка электроточки (Р — розетка, S — выключатель, Св — светильник, ЭВ — вывод кабеля); условные обозначения и общие указания — лист 3.

					Проект: Четырёхкомнатная квартира	М 1:20
	Лист	№ док.	Подпись	Дата		
Дизайнер	Кырлан А.С.			04.11.26	Привязки электроточек, стена А. Зал (пом. 1)	Стадия: П; Лист: 54; Листов: 120

Развёртка стены Б


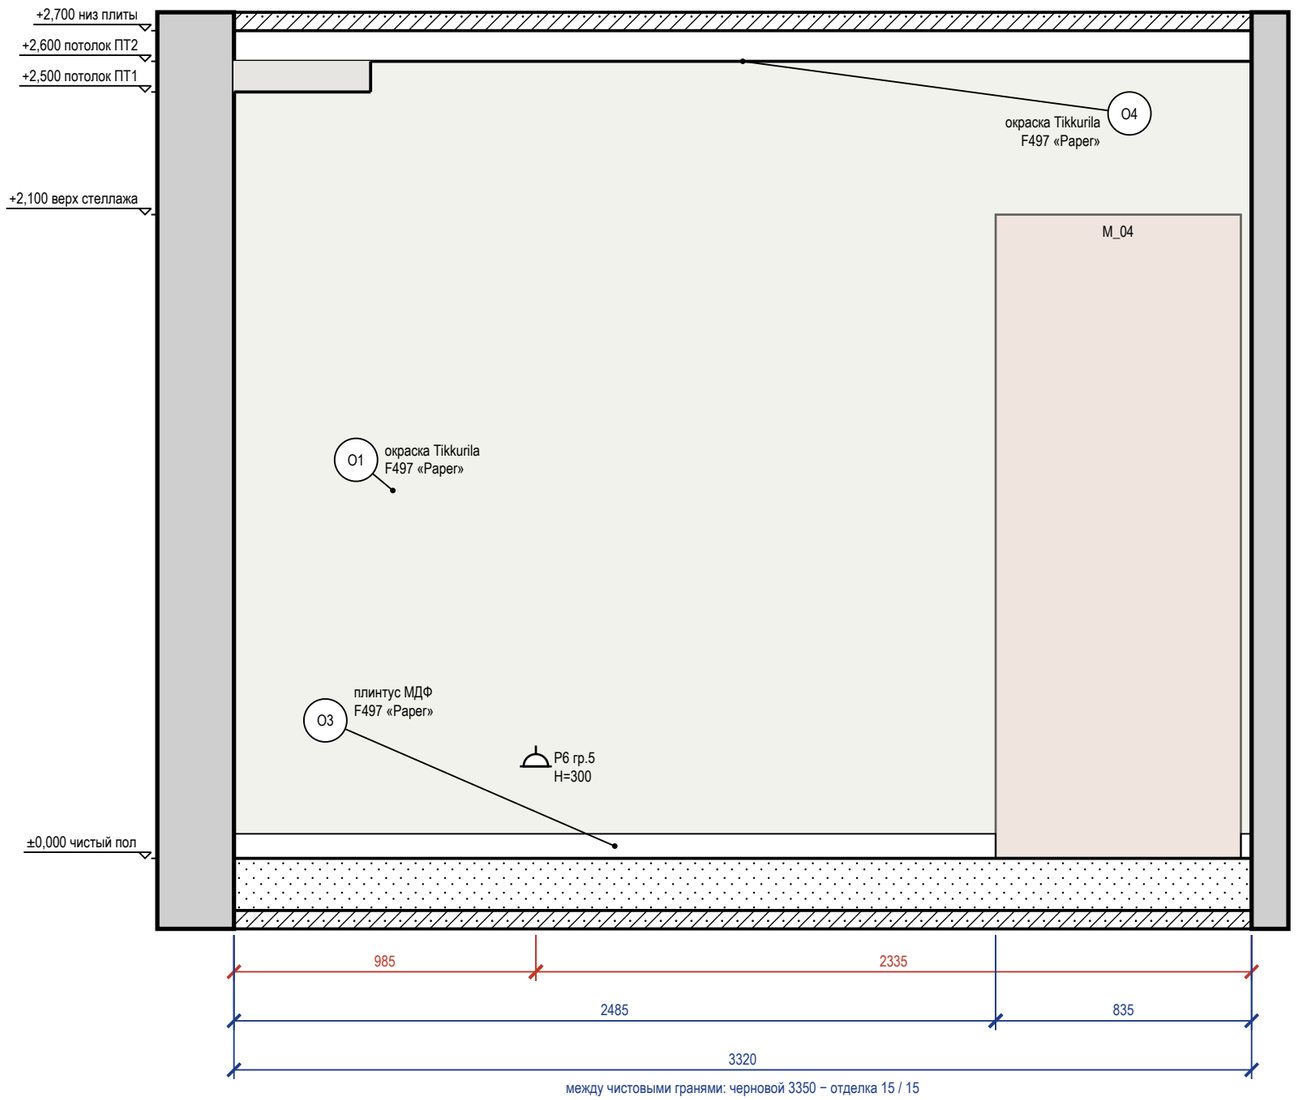


Схема развёрток (М 1:100)

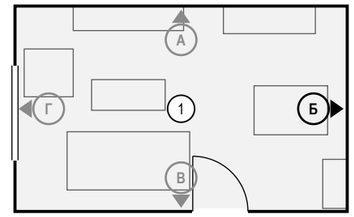

Ведомость отделки (на листе)

Марка	Поверхность	Материал, изделие	Цвет, код	Кол.
О1	стены	окраска, Tikkurila Optiva 5 Matt, матовая, подготовка К3	Tikkurila F497 «Paper»	8,6 м²
О3	плинтус	плинтус МДФ, h 80 мм, аналог: плинтус МДФ под окраску 80×16 мм, полуглянцевая	Tikkurila F497 «Paper»	2,5 м
О4	потолок	окраска, Tikkurila Anti-Reflex 2, глубокоматовая, подготовка Q3	Tikkurila F497 «Paper»	18,2 м²

Примечания

1. Размеры — в мм от чистовых поверхностей стен; условные обозначения и общие указания — лист 3.
2. Потолок — у каждой стены свой, по плану потолков (ПТ2, ПТ1); ступени — зоной, кромка короба перед нишей — тонкой линией.

					Проект: Четырёхкомнатная квартира	М 1:20
	Лист	№ док.	Подпись	Дата		
Дизайнер	Кырлан А.С.			04.11.26	Развёртка стены Б. Зал (пом. 1)	Стадия: П; Лист: 55; Листов: 120

Развёртка стены В


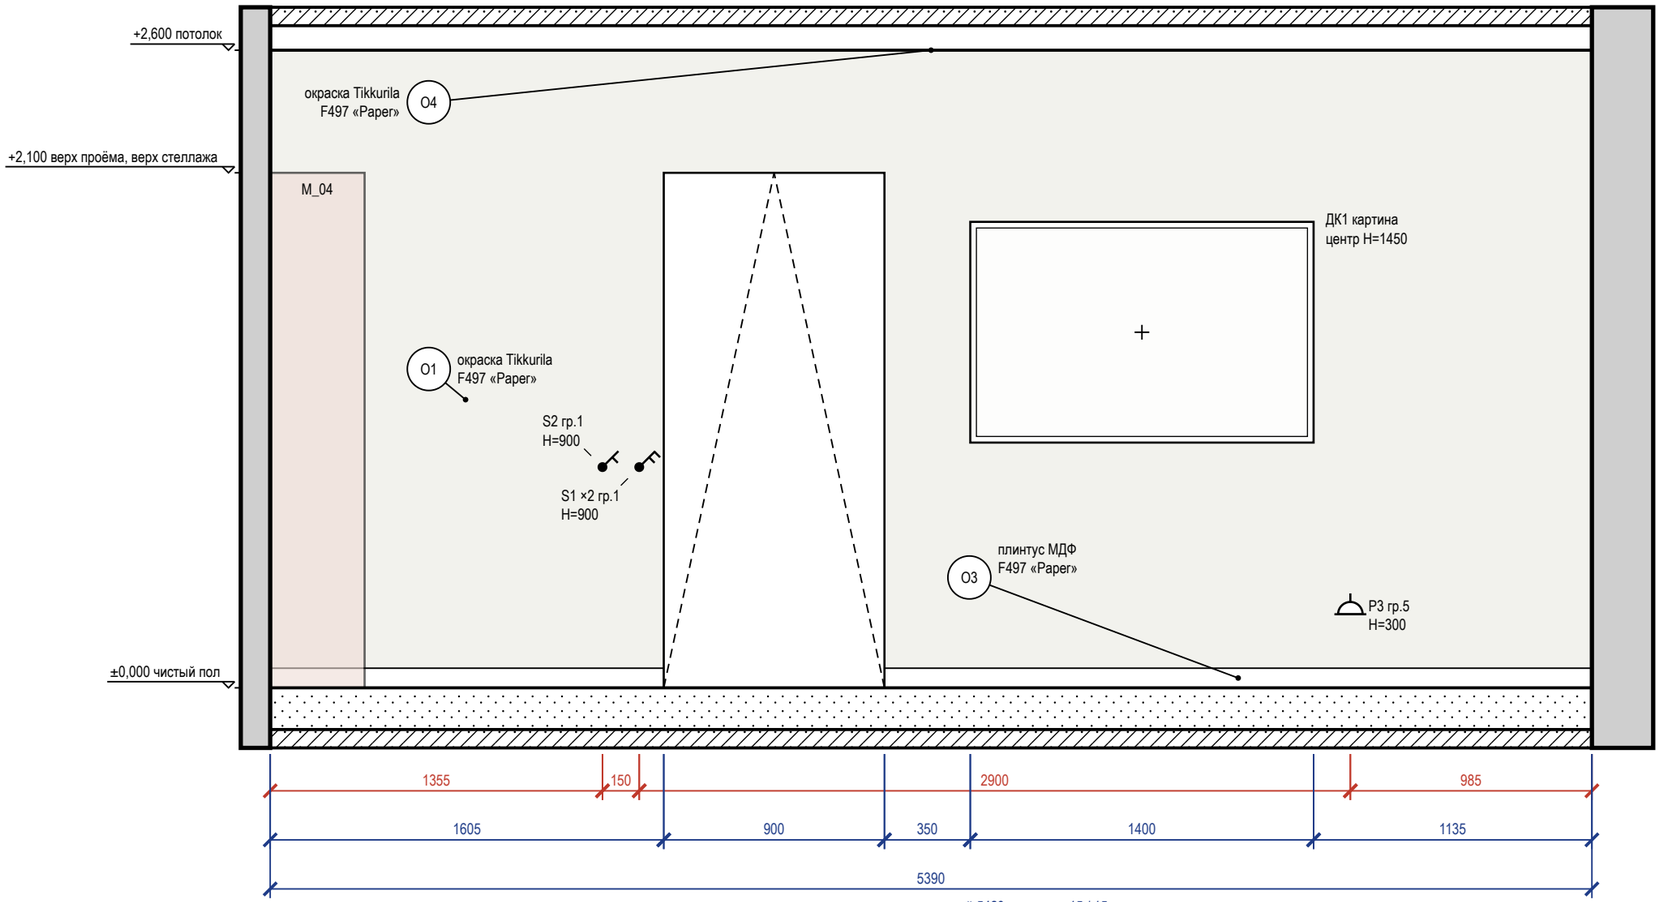


Схема развёрток (М 1:100)

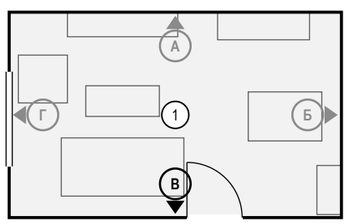

Ведомость отделки (на листе)

Марка	Поверхность	Материал, изделие	Цвет, код	Кол.
O1	стены	окраска, Tikkurila Optiva 5 Matt, матовая, подготовка К3	Tikkurila F497 «Paper»	12,1 м²
O3	плинтус	плинтус МДФ, h 80 мм, аналог: плинтус МДФ под окраску 80×16 мм, полуглянцевая	Tikkurila F497 «Paper»	4,5 м
O4	потолок	окраска, Tikkurila Anti-Reflex 2, глубокоматовая, подготовка Q3	Tikkurila F497 «Paper»	18,2 м²

Примечания

1. Размеры — в мм от чистовых поверхностей стен; условные обозначения и общие указания — лист 3.
2. Картины и зеркала крепить к основанию по паспорту изделия (закладные и анкеры — в перечне скрытых работ); крест — ось центра предмета.
3. Потолок — у каждой стены свой, по плану потолков (ПТ2); ступени — зоной, кромка короба перед нишей — тонкой линией; в поле потолка: ПТ1 +2,500.

					Проект: Четырёхкомнатная квартира	М 1:25
	Лист	№ док.	Подпись	Дата	Развёртка стены В. Зал (пом. 1)	Стадия / Лист / Листов
Дизайнер	Кырлан А.С.			04.11.26		П / 56 / 120

Развёртка стены Г


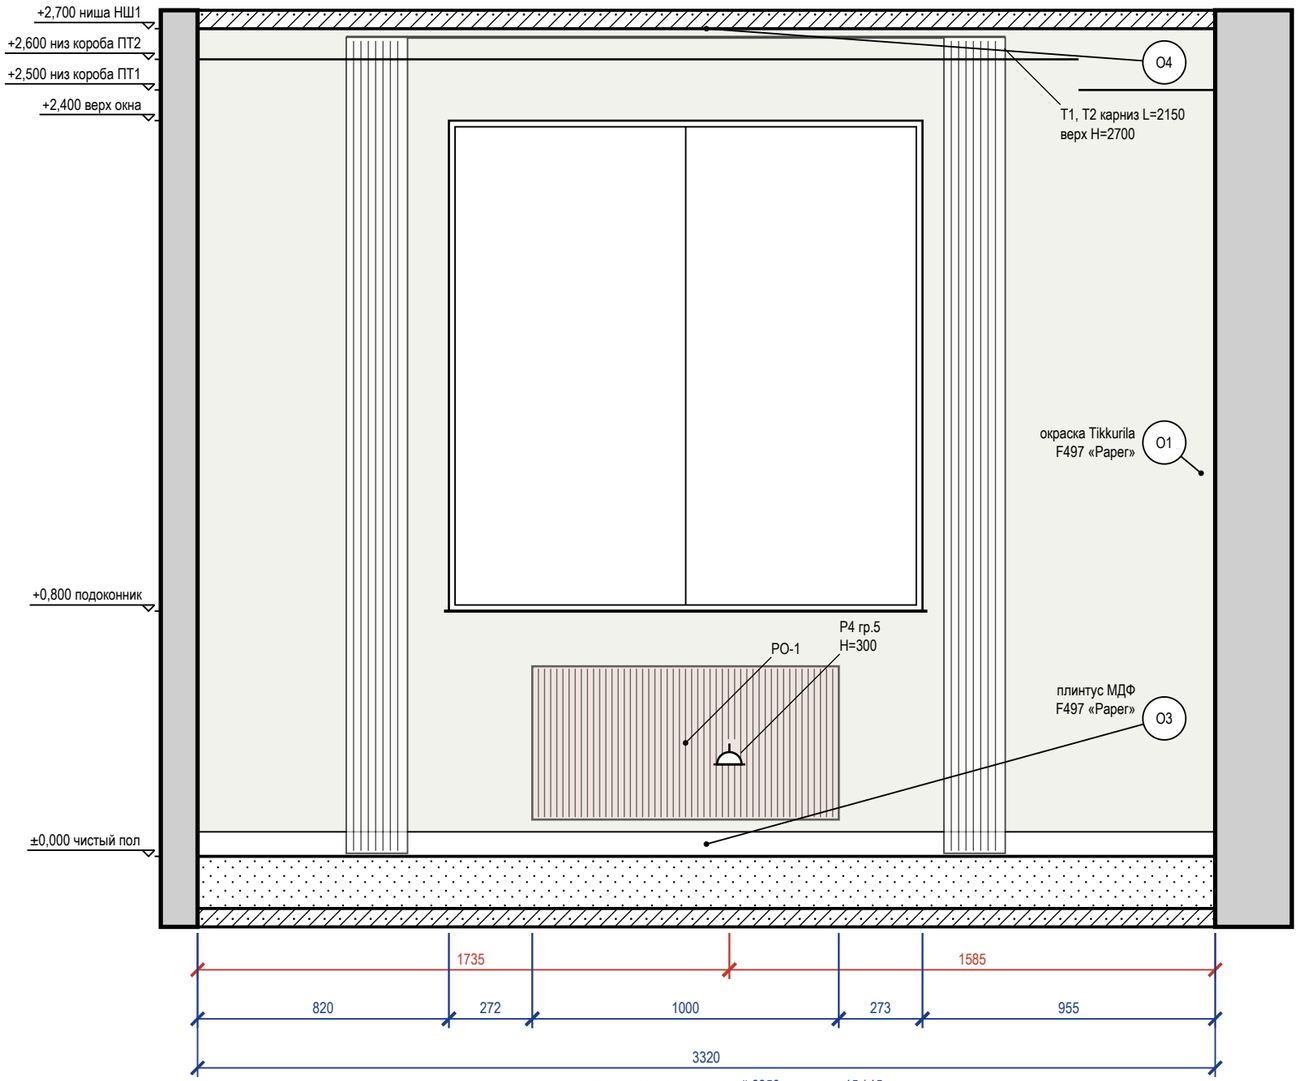


Схема развёрток (М 1:100)

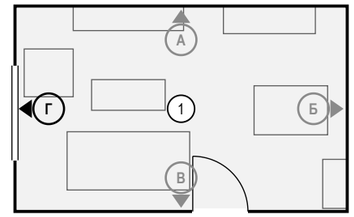

Ведомость отделки (на листе)

Марка	Поверхность	Материал, изделие	Цвет, код	Кол.
О1	стены	окраска, Tikkurila Optiva 5 Matt, матовая, подготовка К3	Tikkurila F497 «Paper»	6,5 м²
О3	плинтус	плинтус МДФ, h 80 мм, аналог: плинтус МДФ под окраску 80×16 мм, полуглянцевая	Tikkurila F497 «Paper»	3,3 м
О4	потолок	окраска, Tikkurila Anti-Reflex 2, глубокоматовая, подготовка Q3	Tikkurila F497 «Paper»	18,2 м²

Примечания

1. Размеры — в мм от чистовых поверхностей стен; условные обозначения и общие указания — лист 3.
2. Карнизы (шины) — по ведомости текстиля декоратора: длина L и верх H на развёртке — те же числа, что в ведомости; крепление — до окраски потолка.
3. Потолок — у каждой стены свой, по плану потолков (НШ1, ПТ2, ПТ1); ступени — зоной, кромка короба перед нишей — тонкой линией.
4. Линии узора (швы плитки, складки штор, рёбра радиаторов) прерываются у знаков и выносок — просвет между линиями не менее 0,7 мм.


	Лист	№ док.	Подпись	Дата
Дизайнер	Кырлан А.С.			04.11.26

Проект: Четырёхкомнатная квартира — М 1:20

Развёртка стены Г. Зал (пом. 1)


Стадия	Лист	Листов
П	57	120

Развёртка стены А

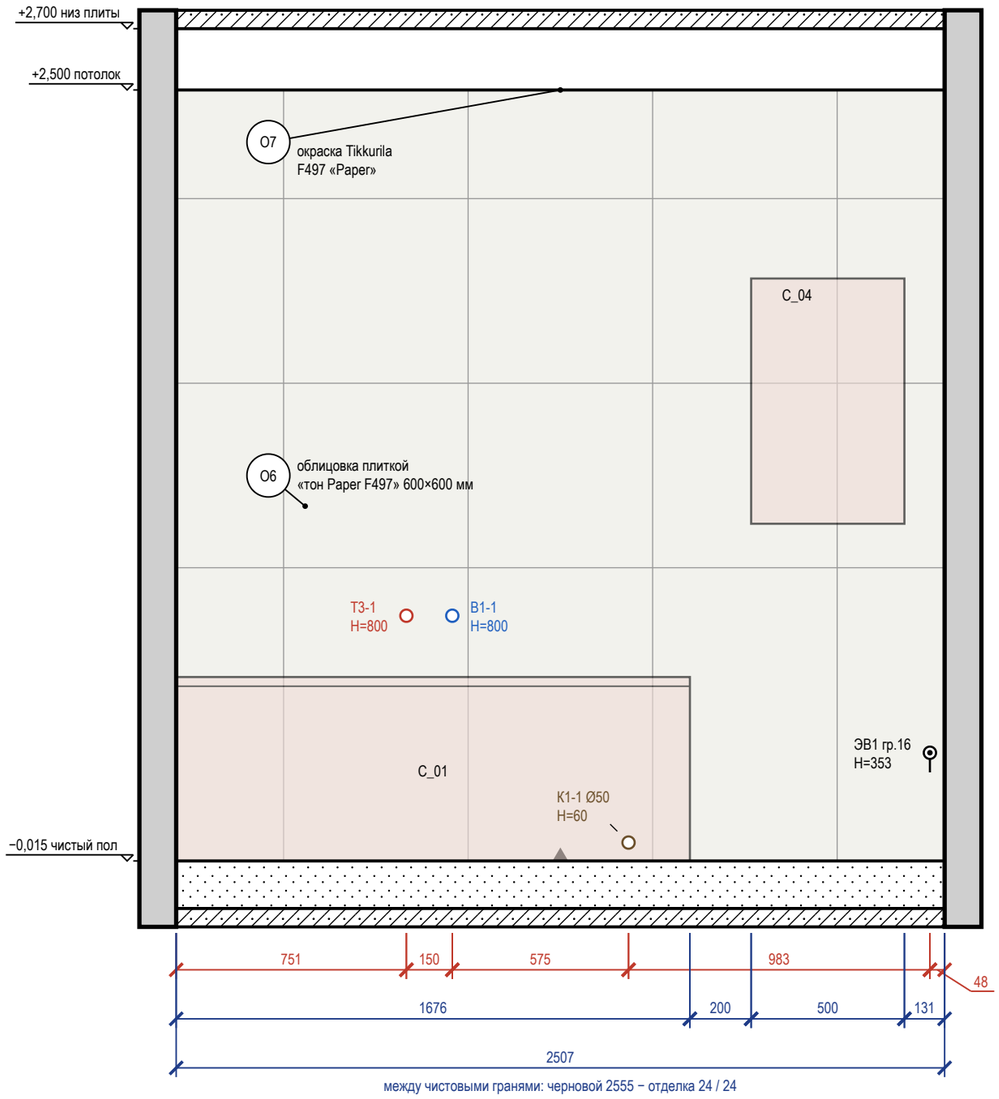


между чистовыми гранями: черновой 2555 − отделка 24 / 24

Развёртка стены Б

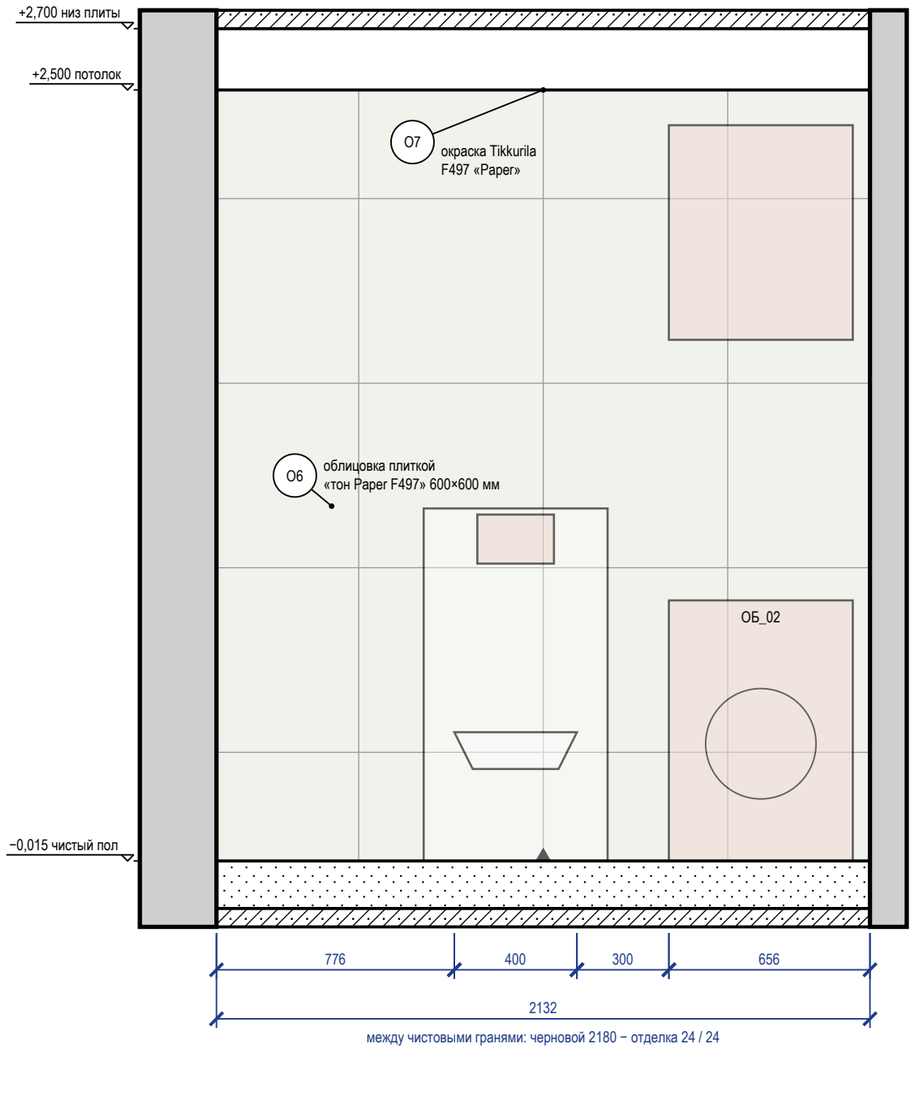

между чистовыми гранями: черновой 2180 − отделка 24 / 24

Схема развёрток (М 1:100)

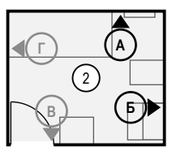

Ведомость отделки (на листе)

Марка	Поверхность	Материал, изделие	Цвет, код	Кол.
О6	стены	облицовка плиткой, 600×600×9 мм, аналог: керамогранит матовый, тон F497, затирка CG2WA	#F1F1EC «тон Paper F497»	11,7 м²
О7	потолок	окраска, Tikkurila Luja 7, матовая, подготовка Q3	Tikkurila F497 «Paper»	5,6 м²


Примечания

1. Размеры — в мм от чистовых поверхностей стен; условные обозначения и общие указания — лист 3.
2. Стена Б показана двумя видами: здесь — архитектурная развёртка (мебель, отделка, проёмы, высоты), электроточки и выводы ВК с привязками и таблицей — на листе 60 («Привязки»).
3. Схема мебели, приборов и декора не является технической документацией для производства мебели; габариты — по паспортам изделий.
4. Облицовка — по сетке швов 2 мм, раскладка от оси стены (треугольник у пола), по высоте — от середины облицовки, подрезки у пола и у потолка поровну; подрезки — по листу раскладки плитки.
5. Гидроизоляция в 2 слоя, заход на стены 200 мм; над ванной — до 2100 и 300 мм за борт — до облицовки, с актом скрытых работ и тестом проливом (узел — на листе узлов).

					Проект: Четырёхкомнатная квартира	М 1:20
	Лист	№ док.	Подпись	Дата	Развёртки стен А, Б. Ванная комната (пом. 2)	
Дизайнер	Кырлан А.С.			04.11.26		


Стадия	Лист	Листов
П	58	120

Развёртка стены В

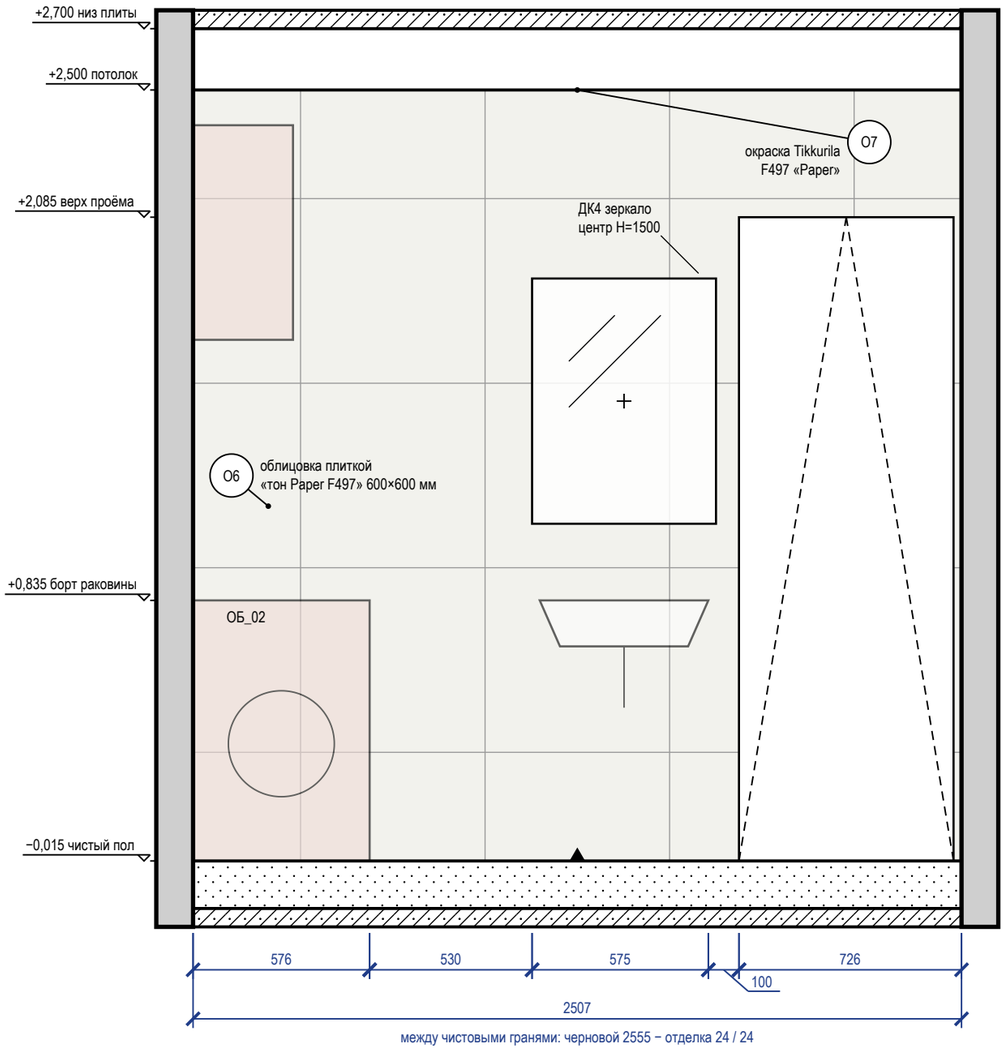


между чистовыми гранями: черновой 2555 − отделка 24 / 24

Развёртка стены Г

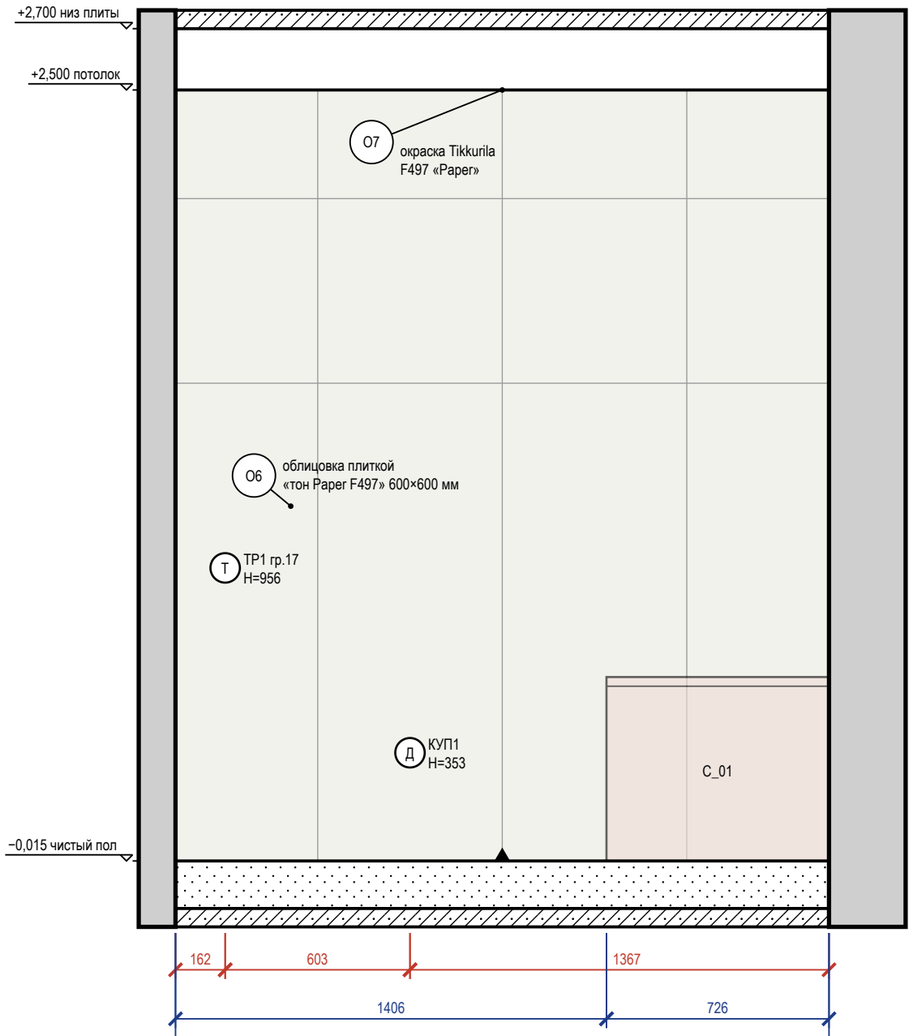

между чистовыми гранями: черновой 2180 − отделка 24 / 24

Схема развёрток (М 1:100)

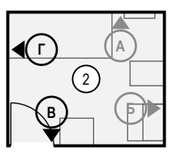

Ведомость отделки (на листе)

Марка	Поверхность	Материал, изделие	Цвет, код	Кол.
О6	стены	облицовка плиткой, 600×600×9 мм, аналог: керамогранит матовый, тон F497, затирка CG2WA	#F1F1EC «тон Paper F497»	10,2 м²
О7	потолок	окраска, Tikkurila Luja 7, матовая, подготовка Q3	Tikkurila F497 «Paper»	5,6 м²


Примечания

1. Размеры — в мм от чистовых поверхностей стен; условные обозначения и общие указания — лист 3.
2. Стена В показана двумя видами: здесь — архитектурная развёртка (мебель, отделка, проёмы, высоты), электроточки и выводы ВК с привязками и таблицей — на листе 60 («Привязки»).
3. Схема мебели, приборов и декора не является технической документацией для производства мебели; габариты — по паспортам изделий.
4. Облицовка — по сетке швов 2 мм, раскладка от оси стены (треугольник у пола), по высоте — от середины облицовки, подрезки у пола и у потолка поровну; подрезки — по листу раскладки плитки.
5. Гидроизоляция в 2 слоя, заход на стены 200 мм; над ванной — до 2100 и 300 мм за борт — до облицовки, с актом скрытых работ и тестом проливом (узел — на листе узлов).
6. Картины и зеркала крепить к основанию по паспорту изделия (закладные и анкеры — в перечне скрытых работ); крест — ось центра предмета.

					Проект: Четырёхкомнатная квартира — М 1:20
	Лист	№ док.	Подпись	Дата	Развёртки стен В, Г. Ванная комната (пом. 2)
Дизайнер	Кырлан А.С.			04.11.26	

Стадия	Лист	Листов
П	59	120

Развёртка стены Б: электроточки и выводы

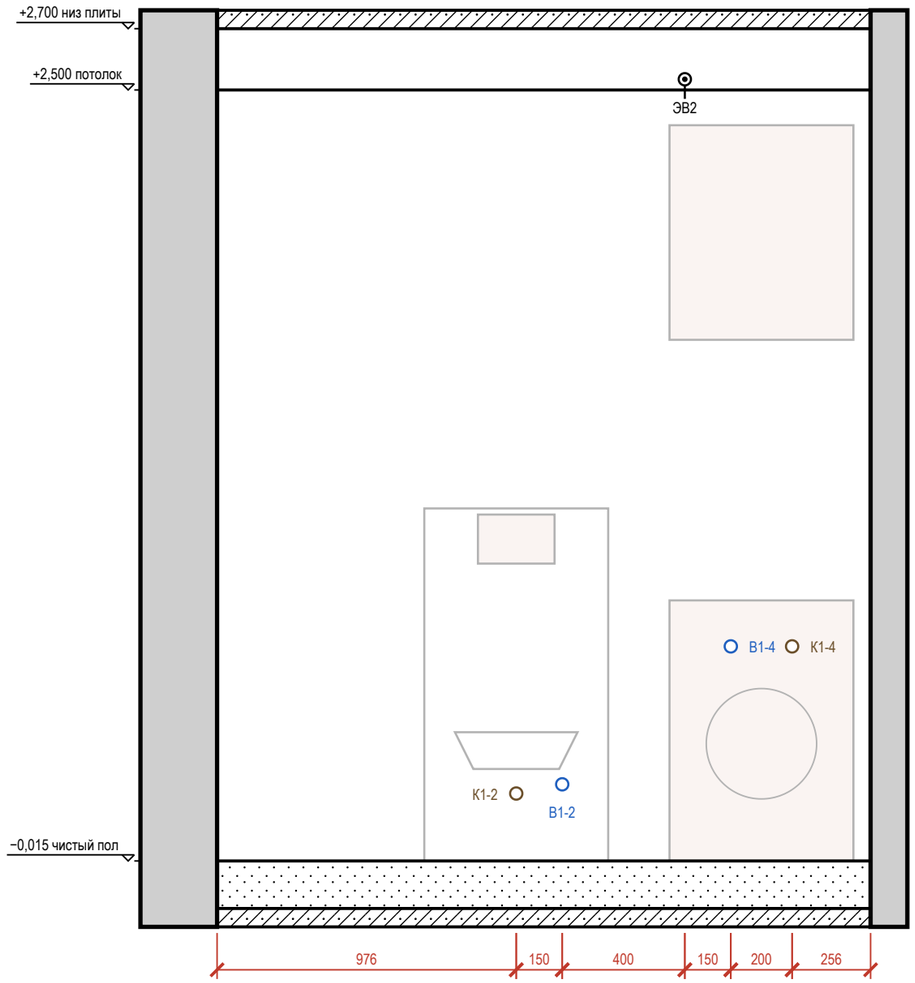

Развёртка стены В: электроточки и выводы

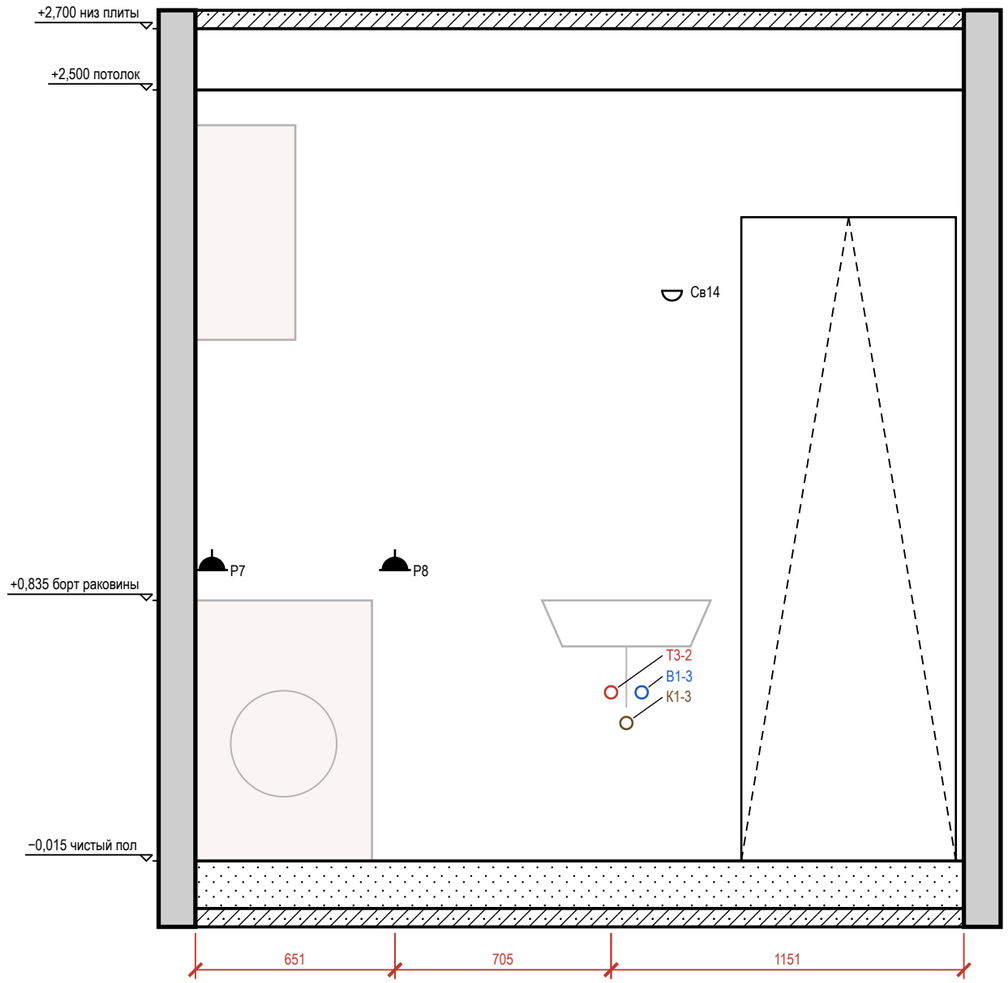


Таблица привязок электроточек и выводов

Стена	Марка	Назначение	От угла, мм	Н от пола, мм	Примечание
Б	К1-2	канализация — унитаз подвесной	976	220	Ø110
Б	В1-2	холодная вода — унитаз подвесной	1126	250	в раме инсталляции
Б	ЭВ2	вывод кабеля: вентилятор ВР1 (таймер выбега)	1526	2550	гр. 4
Б	В1-4	холодная вода — стиральная машина	1676	700	кран машины
Б	К1-4	канализация — стиральная машина	1876	700	Ø40
В	Р7	розетка: стиральная машина	48	949	гр. 14, IP44

Стена	Марка	Назначение	От угла, мм	Н от пола, мм	Примечание
В	Р8	розетка: фен у умывальника	651	949	гр. 15, IP44
В	Т3-2	горячая вода — умывальник	1356	550	межос. 100
В	К1-3	канализация — умывальник	1406	450	Ø40
В	В1-3	холодная вода — умывальник	1456	550	межос. 100
В	Св14	светильник настенный	1555	1860	гр. 4

Условные обозначения

- розетка влагозащищённая IP44
- вывод кабеля для подключения прибора (без розетки), марка ЭВ
- светильник настенный (бра), Н — высота оси
- вывод В1 (код — в ведомости привязок)
- вывод Т3 (код — в ведомости привязок)
- вывод К1 (код — в ведомости привязок)
- привязки точек и выводов от угла и от пола, мм


Примечания

1. Вид «Привязки» стен Б, В — электроточки и выводы ВК; архитектурная развёртка (мебель, отделка, проёмы, высоты) — на листах 58, 59. Мебель и приборы подложкой для ориентира; их марки и обозначения мебели, проёмов и стен — там же.
2. Привязки — в мм: по горизонтали от левого чистового угла стены до оси изделия, Н — от чистого пола до оси; все точки — в таблице привязок. Красная цепочка — привязки по осям; точки ближе 120 мм одна к другой в цепочку не дробятся — их привязки только в таблице.
3. У знака — марка электроточки (Р — розетка, S — выключатель, Св — светильник, ЭВ — вывод кабеля); условные обозначения и общие указания — лист 3.
4. Коды выводов ВК: В1 — холодная вода, Т3 — горячая вода, К1 — канализация; номер после дефиса — номер вывода на листе выводов сантехники.


					Проект: Четырёхкомнатная квартира — **М 1:20**
	Лист	№ док.	Подпись	Дата	Привязки электроточек и выводов ВК, стены Б, В. Ванная комната (пом. 2)
Дизайнер	Кырлан А.С.			04.11.26	

Стадия	Лист	Листов
П	60	120

Развёртка стены А

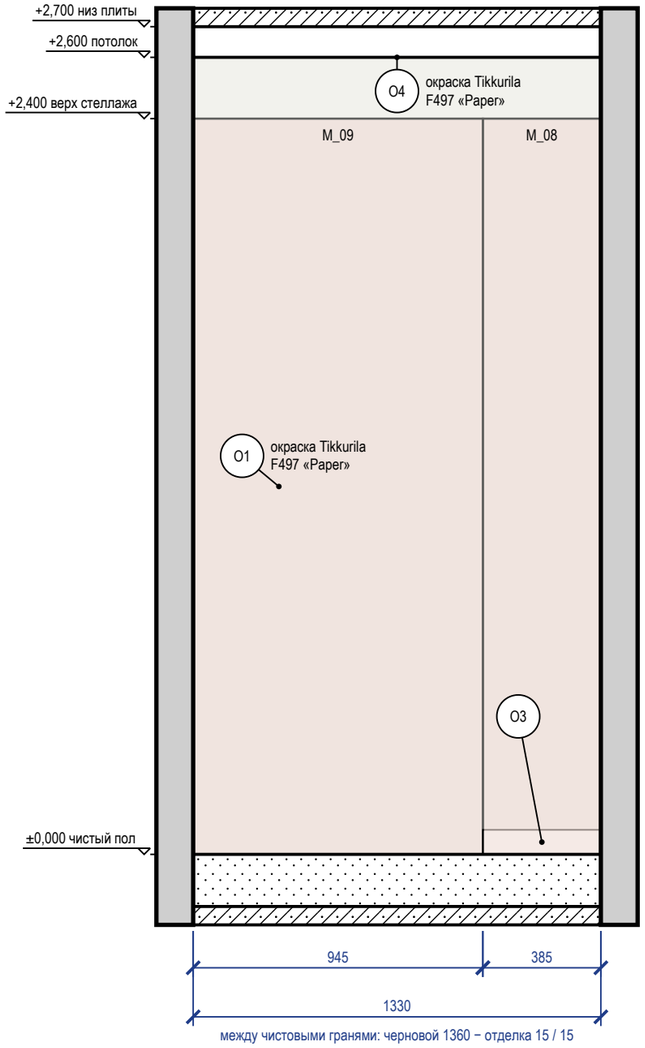

Развёртка стены Б

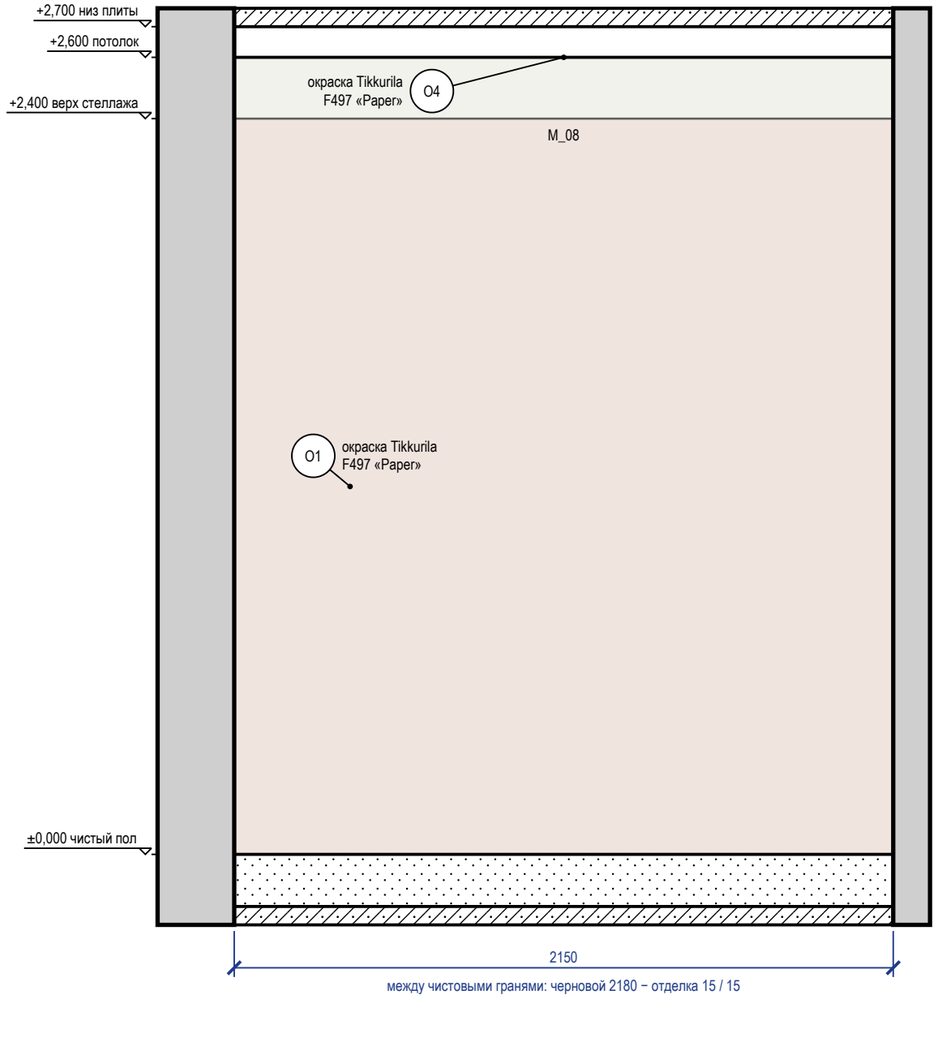

Развёртка стены В


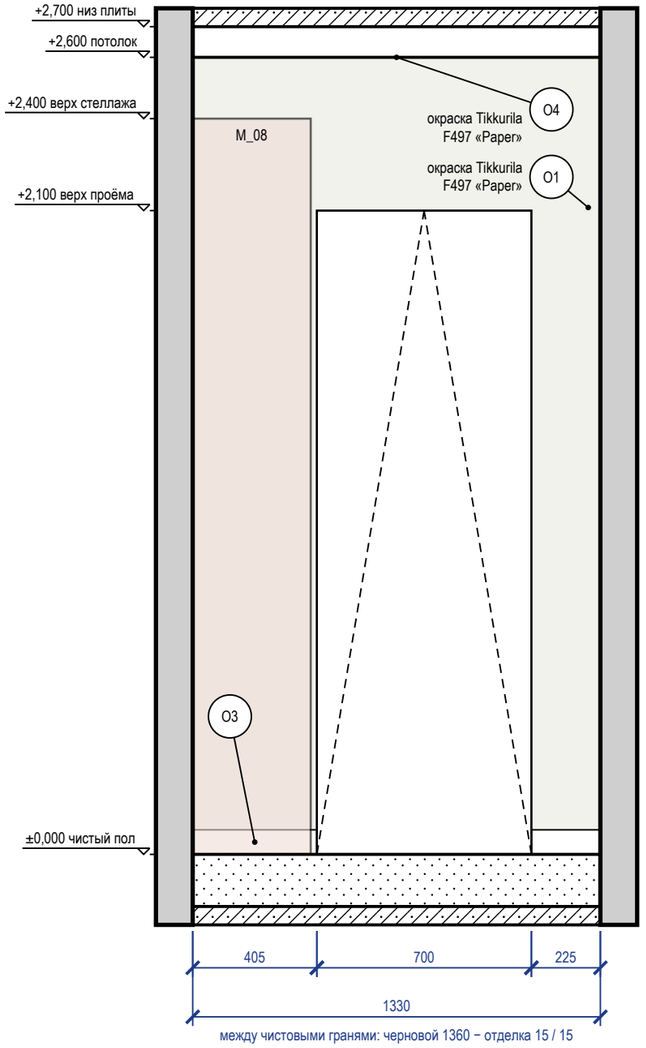


Схема развёрток (М 1:100)

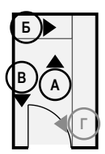

Ведомость отделки (на листе)

Марка	Поверхность	Материал, изделие	Цвет, код	Кол.
O1	стены	окраска, Tikkurila Optiva 5 Matt, матовая, подготовка К3	Tikkurila F497 «Paper»	11 м²
O3	плинтус	плинтус МДФ, h 80 мм, аналог: плинтус МДФ под окраску 80×16 мм, полуглянцевая	Tikkurila F497 «Paper»	1 м
O4	потолок	окраска, Tikkurila Anti-Reflex 2, глубокоматовая, подготовка Q3	Tikkurila F497 «Paper»	3 м²

Примечания

1. Размеры — в мм от чистовых поверхностей стен; условные обозначения и общие указания — лист 3.

					Проект: Четырёхкомнатная квартира	М 1:20
	Лист	№ док.	Подпись	Дата	Развёртки стен А, Б, В. Тёмная комната (пом. 3)	Стадия / Лист / Листов
Дизайнер	Кырлан А.С.			04.11.26		П / 61 / 120

выпуск 04.11.2026 № 2391fcbada · стр. 61 из 120

Развёртка стены Г


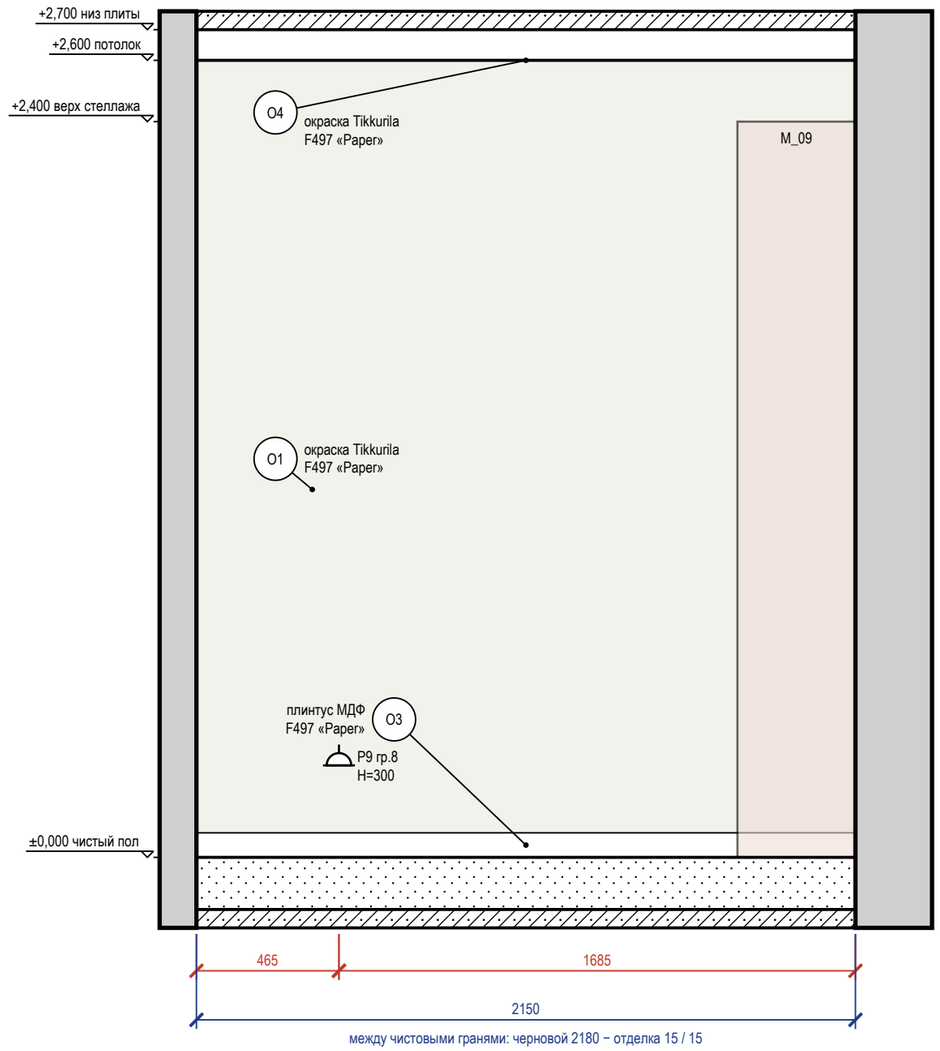


Схема развёрток (М 1:100)

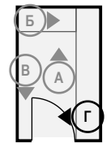

Ведомость отделки (на листе)

Марка	Поверхность	Материал, изделие	Цвет, код	Кол.
О1	стены	окраска, Tikkurila Optiva 5 Matt, матовая, подготовка К3	Tikkurila F497 «Paperг»	5,6 м²
О3	плинтус	плинтус МДФ, h 80 мм, аналог: плинтус МДФ под окраску 80×16 мм, полуглянцевая	Tikkurila F497 «Paperг»	2,1 м
О4	потолок	окраска, Tikkurila Anti-Reflex 2, глубокоматовая, подготовка Q3	Tikkurila F497 «Paperг»	3 м²

Примечания

1. Размеры — в мм от чистовых поверхностей стен; условные обозначения и общие указания — лист 3.

					Проект: Четырёхкомнатная квартира	М 1:20
	Лист	№ док.	Подпись	Дата		
Дизайнер	Кырлан А.С.			04.11.26	Развёртка стены Г. Тёмная комната (пом. 3)	Стадия: П; Лист: 62; Листов: 120

Развёртка стены А


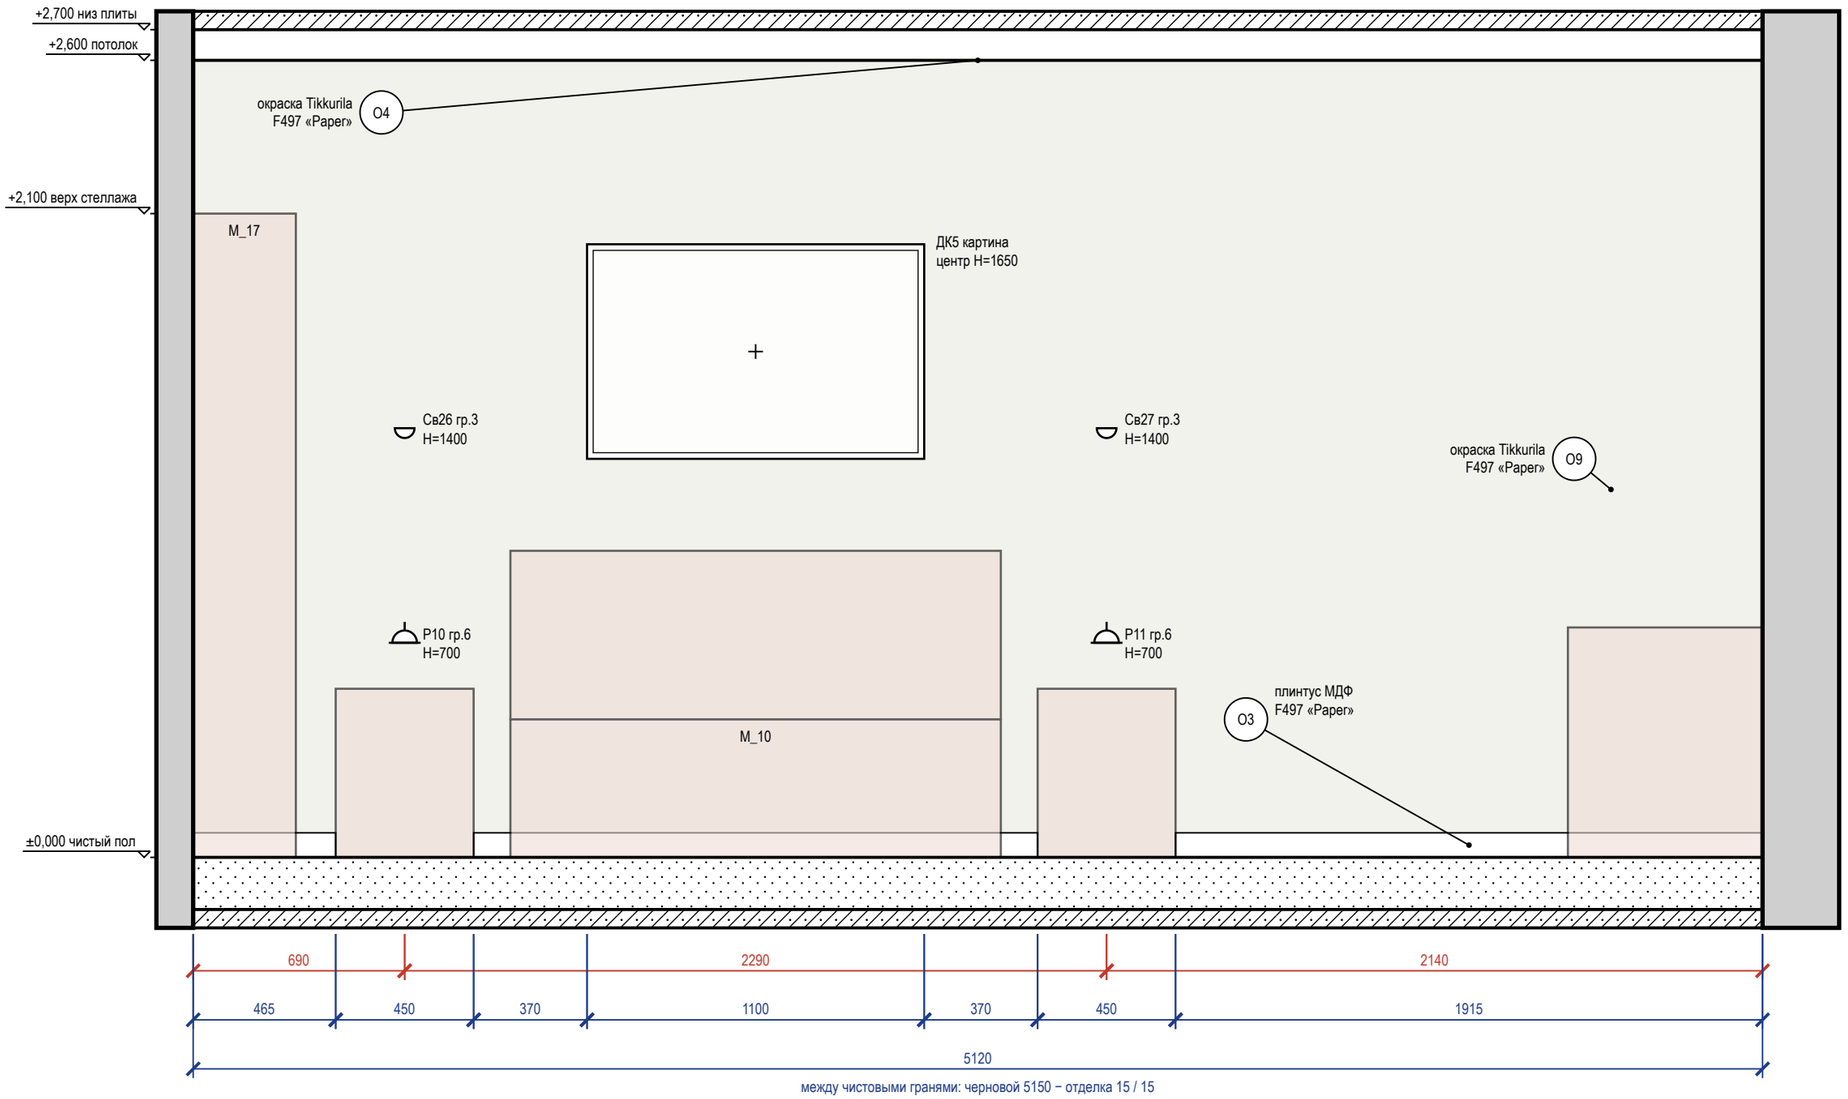


Схема развёрток (М 1:100)

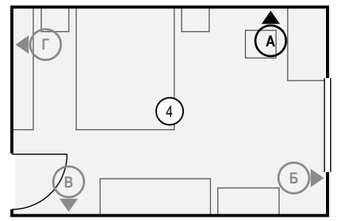

Ведомость отделки (на листе)

Марка	Поверхность	Материал, изделие	Цвет, код	Кол.
О3	плинтус	плинтус МДФ, h 80 мм, аналог: плинтус МДФ под окраску 80×16 мм, полуглянцевая	Tikkurila F497 «Paper»	4,2 м
О4	потолок	окраска, Tikkurila Anti-Reflex 2, глубокоматовая, подготовка Q3	Tikkurila F497 «Paper»	17,5 м²
О9	стены	окраска, Tikkurila Joker, шелковисто-матовая, подготовка К3	Tikkurila F497 «Paper»	13,3 м²

Примечания

1. Размеры — в мм от чистовых поверхностей стен; условные обозначения и общие указания — лист 3.
2. Картины и зеркала крепить к основанию по паспорту изделия (закладные и анкеры — в перечне скрытых работ); крест — ось центра предмета.

	Лист	№ док.	Подпись	Дата
Дизайнер	Кырлан А.С.			04.11.26

Проект: Четырёхкомнатная квартира — М 1:20

Развёртка стены А. Детская 1 (пом. 4)

Стадия	Лист	Листов
П	63	120

выпуск 04.11.2026 № 2391fcbada · стр. 63 из 120

Развёртка стены Б


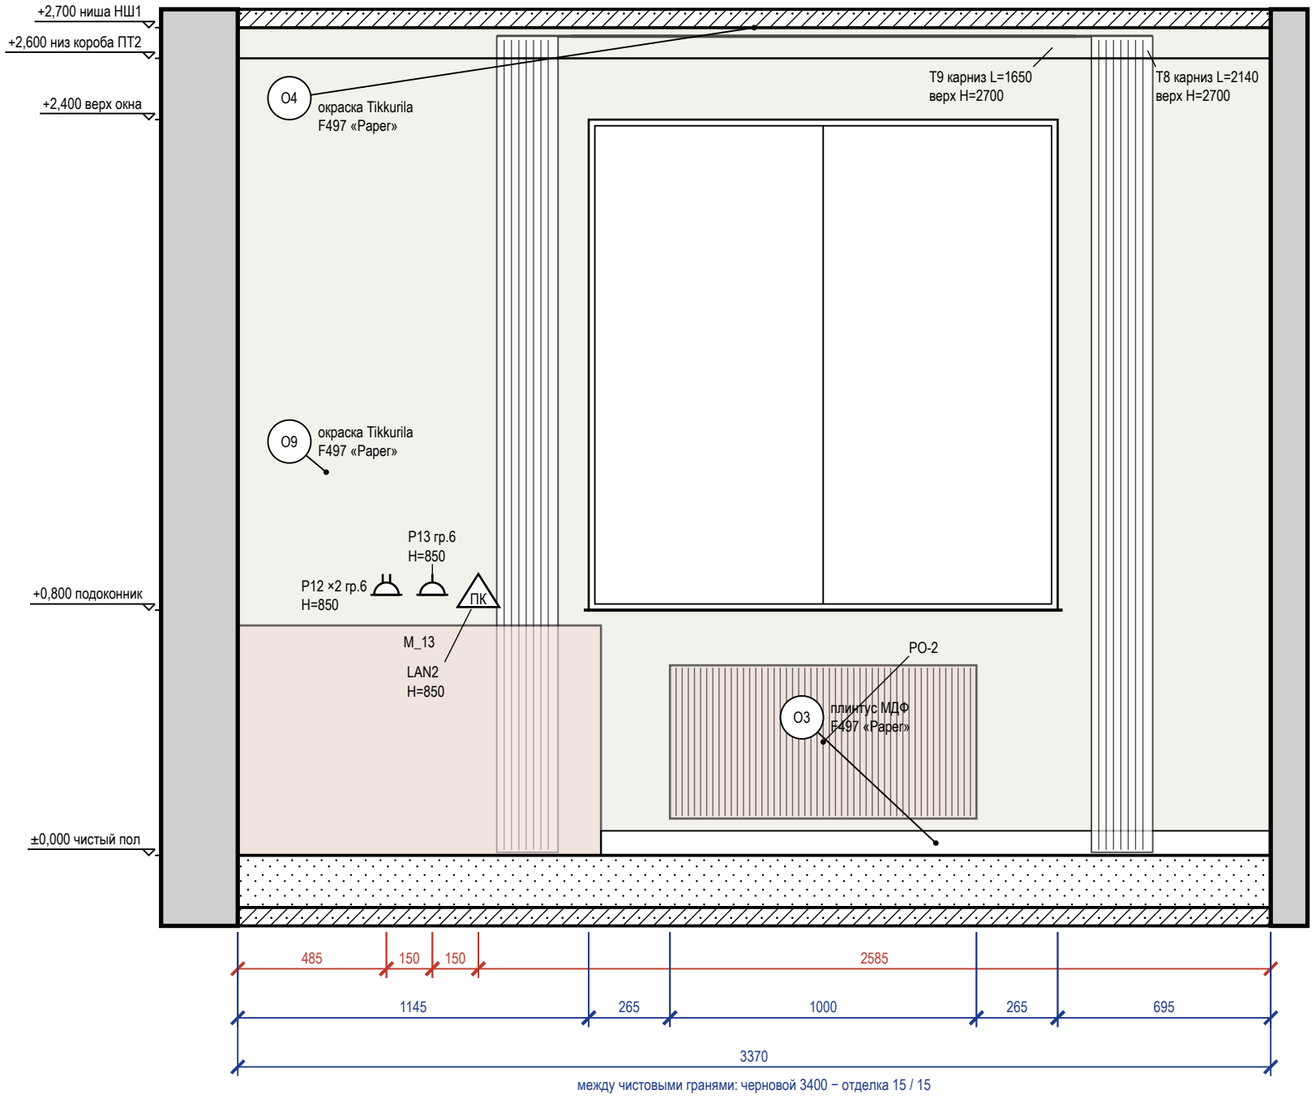


Схема развёрток (М 1:100)

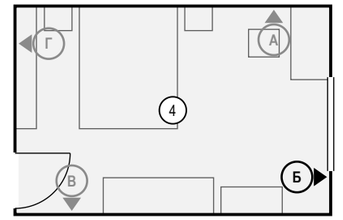

Ведомость отделки (на листе)

Марка	Поверхность	Материал, изделие	Цвет, код	Кол.
О3	плинтус	плинтус МДФ, h 80 мм, аналог: плинтус МДФ под окраску 80×16 мм, полуглянцевая	Tikkurila F497 «Paper»	2,2 м
О4	потолок	окраска, Tikkurila Anti-Reflex 2, глубокоматовая, подготовка Q3	Tikkurila F497 «Paper»	17,5 м²
О9	стены	окраска, Tikkurila Joker, шелковисто-матовая, подготовка К3	Tikkurila F497 «Paper»	6,7 м²

Примечания

1. Размеры — в мм от чистовых поверхностей стен; условные обозначения и общие указания — лист 3.
2. Карнизы (шины) — по ведомости текстиля декоратора: длина L и верх H на развёртке — те же числа, что в ведомости; крепление — до окраски потолка.

					Проект: Четырёхкомнатная квартира — М 1:20
	Лист	№ док.	Подпись	Дата	
Дизайнер	Кырлан А.С.			04.11.26	Развёртка стены Б. Детская 1 (пом. 4)

Стадия	Лист	Листов
П	64	120

Развёртка стены В


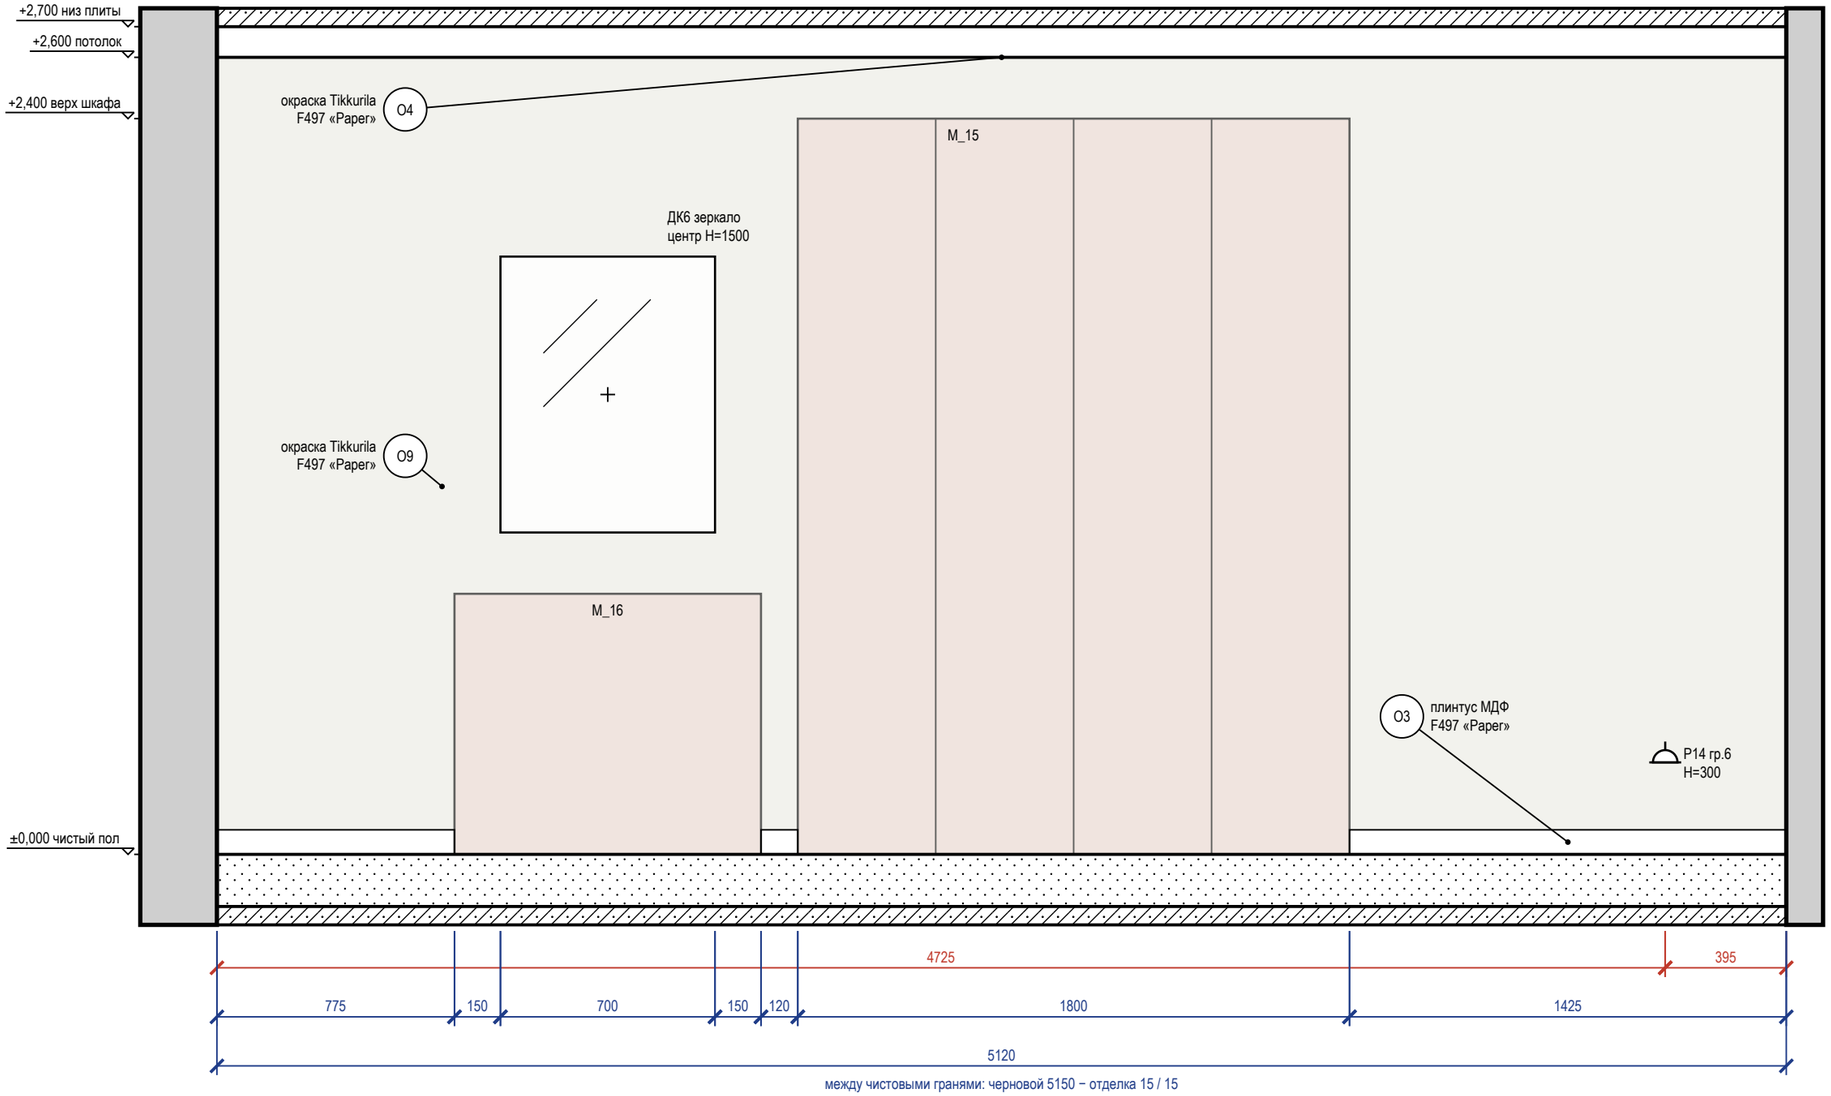


Схема развёрток (М 1:100)

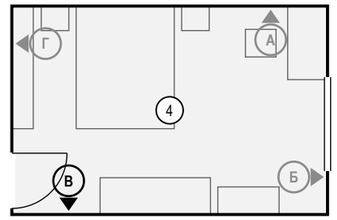

Ведомость отделки (на листе)

Марка	Поверхность	Материал, изделие	Цвет, код	Кол.
О3	плинтус	плинтус МДФ, h 80 мм, аналог: плинтус МДФ под окраску 80×16 мм, полуглянцевая	Tikkurila F497 «Paper»	2,3 м
О4	потолок	окраска, Tikkurila Anti-Reflex 2, глубокоматовая, подготовка Q3	Tikkurila F497 «Paper»	17,5 м²
О9	стены	окраска, Tikkurila Joker, шелковисто-матовая, подготовка К3	Tikkurila F497 «Paper»	13,3 м²

Примечания

1. Размеры — в мм от чистовых поверхностей стен; условные обозначения и общие указания — лист 3.
2. Картины и зеркала крепить к основанию по паспорту изделия (закладные и анкеры — в перечне скрытых работ); крест — ось центра предмета.


	Лист	№ док.	Подпись	Дата
Дизайнер	Кырлан А.С.			04.11.26

Проект: Четырёхкомнатная квартира — М 1:20

Развёртка стены В. Детская 1 (пом. 4)


Стадия	Лист	Листов
П	65	120

Развёртка стены Г

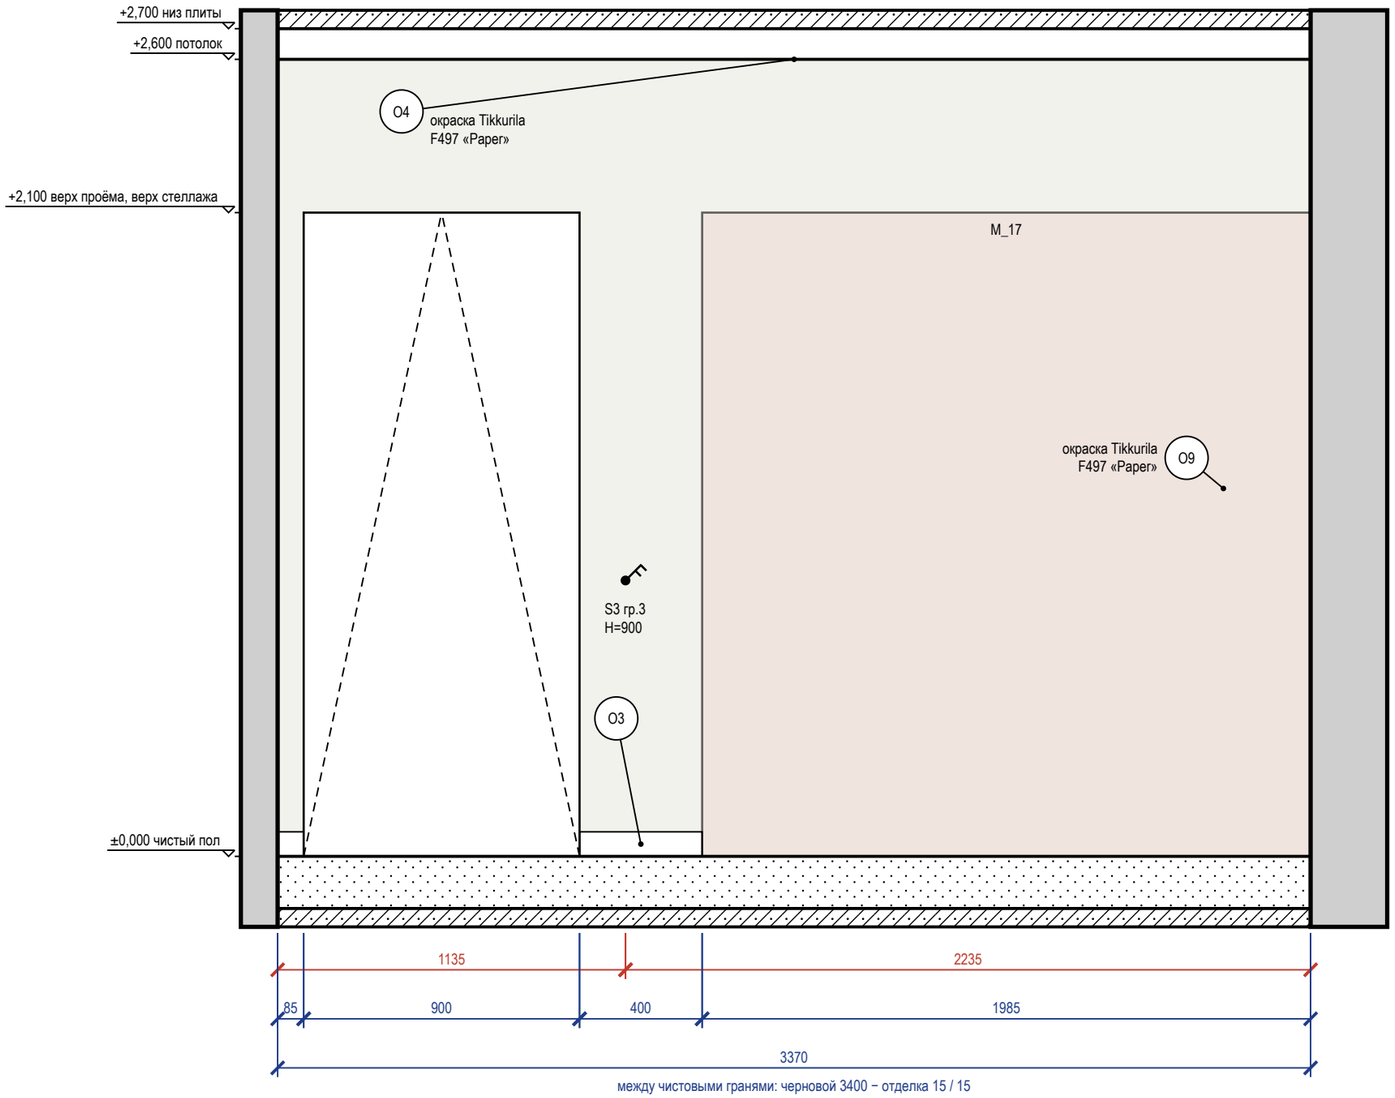

между чистовыми гранями: черновой 3400 − отделка 15 / 15

Схема развёрток (М 1:100)

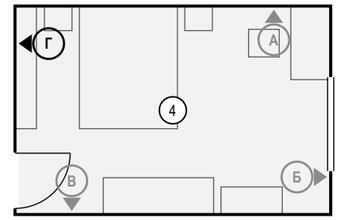

Ведомость отделки (на листе)


Марка	Поверхность	Материал, изделие	Цвет, код	Кол.
О3	плинтус	плинтус МДФ, h 80 мм, аналог: плинтус МДФ под окраску 80×16 мм, полуглянцевая	Tikkurila F497 «Paper»	0,5 м
О4	потолок	окраска, Tikkurila Anti-Reflex 2, глубокоматовая, подготовка Q3	Tikkurila F497 «Paper»	17,5 м²
О9	стены	окраска, Tikkurila Joker, шелковисто-матовая, подготовка К3	Tikkurila F497 «Paper»	6,9 м²

Примечания

1. Размеры — в мм от чистовых поверхностей стен; условные обозначения и общие указания — лист 3.


					Проект: Четырёхкомнатная квартира	М 1:20
	Лист	№ док.	Подпись	Дата		
Дизайнер	Кырлан А.С.			04.11.26	Развёртка стены Г. Детская 1 (пом. 4)	Стадия: П; Лист: 66; Листов: 120

Развёртка стены А

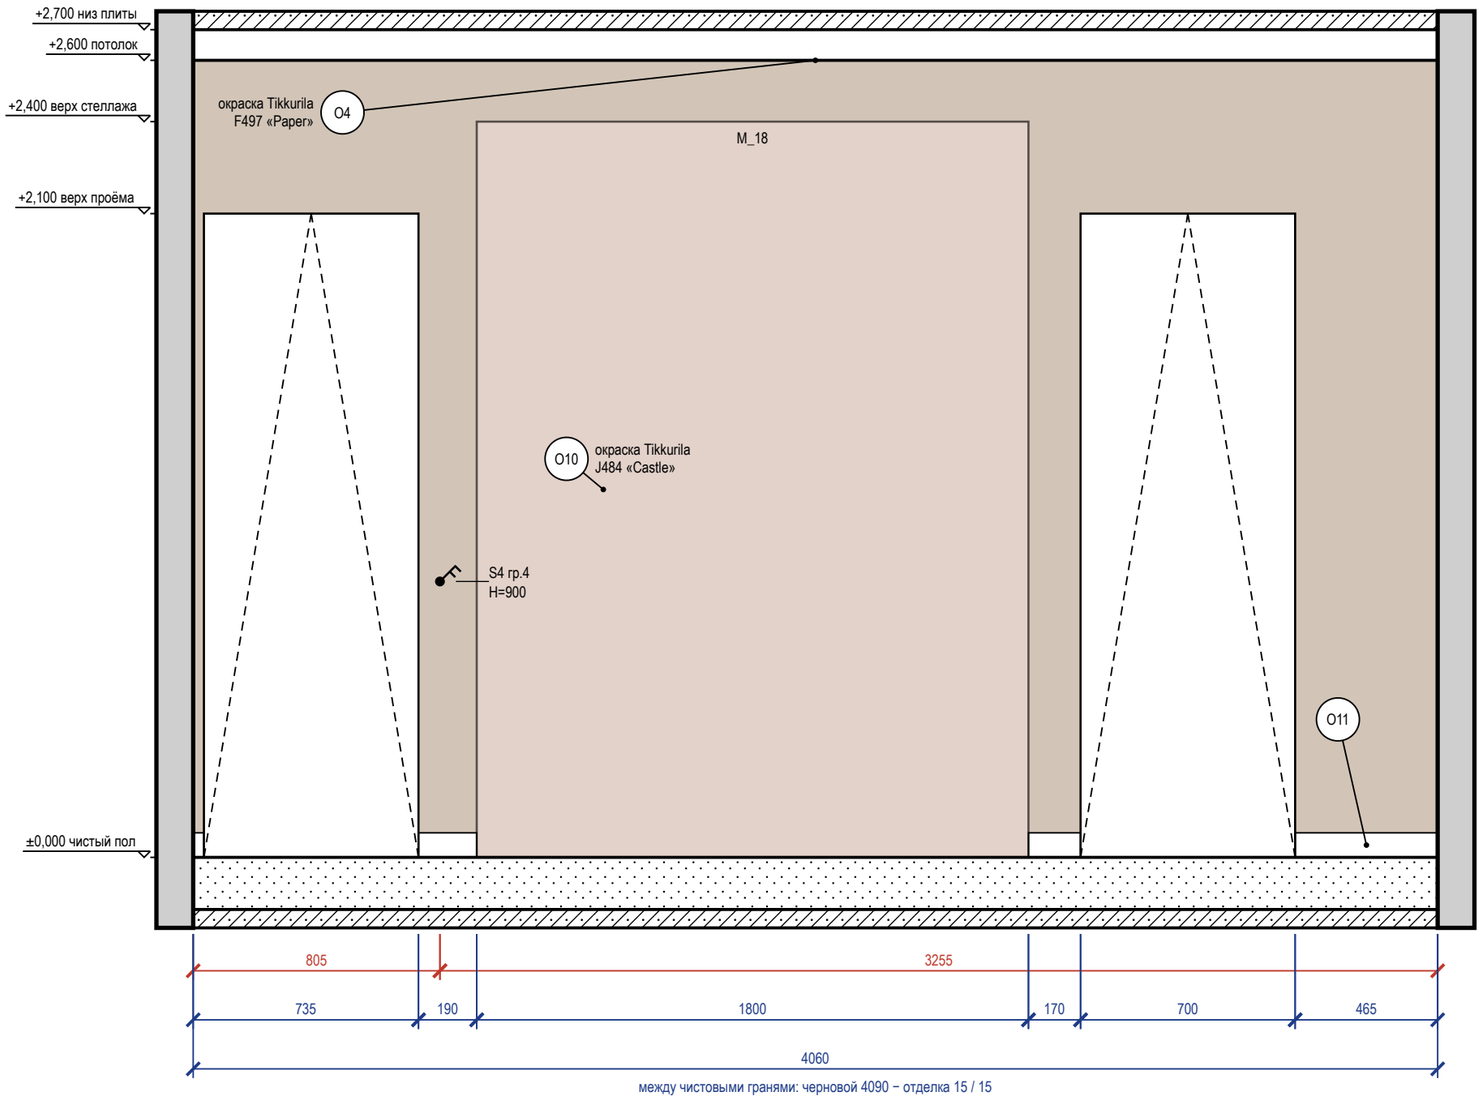


между чистовыми гранями: черновой 4090 − отделка 15 / 15

Развёртка стены Б

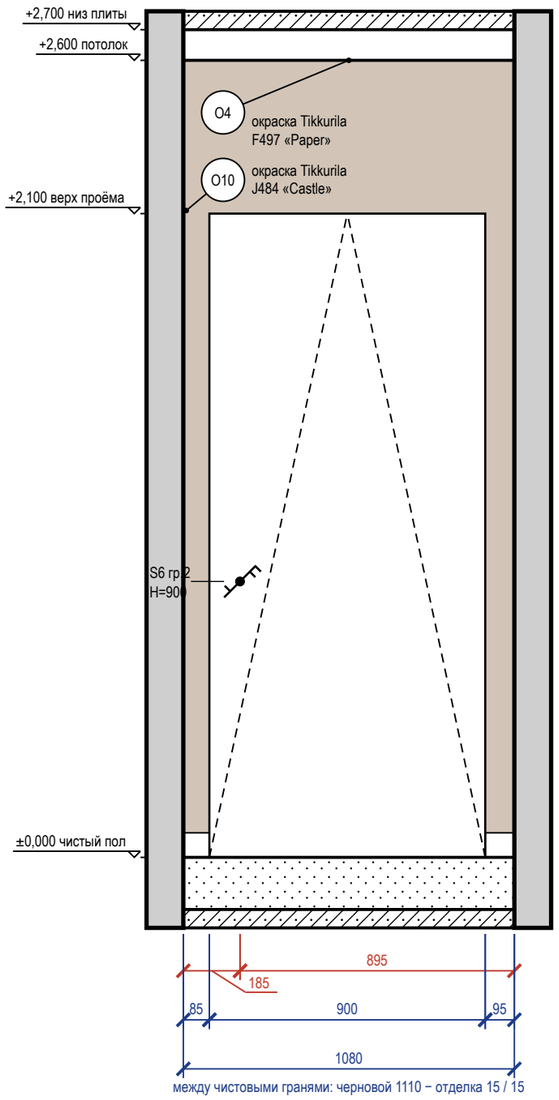

между чистовыми гранями: черновой 1110 − отделка 15 / 15

Схема развёрток (М 1:100)

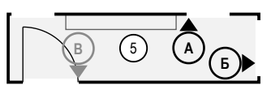

Ведомость отделки (на листе)

Марка	Поверхность	Материал, изделие	Цвет, код	Кол.
O4	потолок	окраска, Tikkurila Anti-Reflex 2, глубокоматовая, подготовка Q3	Tikkurila F497 «Paper»	4,5 м²
O10	стены	окраска, Tikkurila Optiva 20 Semimatt, шелковисто-матовая, подготовка К3	Tikkurila J484 «Castle»	8,5 м²
O11	плинтус	плинтус МДФ, h 80 мм, аналог: плинтус МДФ под окраску 80×16 мм, полуглянцевая	Tikkurila J484 «Castle»	1 м

Примечания

1. Размеры — в мм от чистовых поверхностей стен; условные обозначения и общие указания — лист 3.

	Лист	№ док.	Подпись	Дата
Дизайнер	Кырлан А.С.			04.11.26

Проект: Четырёхкомнатная квартира — М 1:20

Развёртки стен А, Б. Коридор (пом. 5)

Стадия	Лист	Листов
П	67	120

выпуск 04.11.2026 № 2391fcbada · стр. 67 из 120

Развёртка стены В


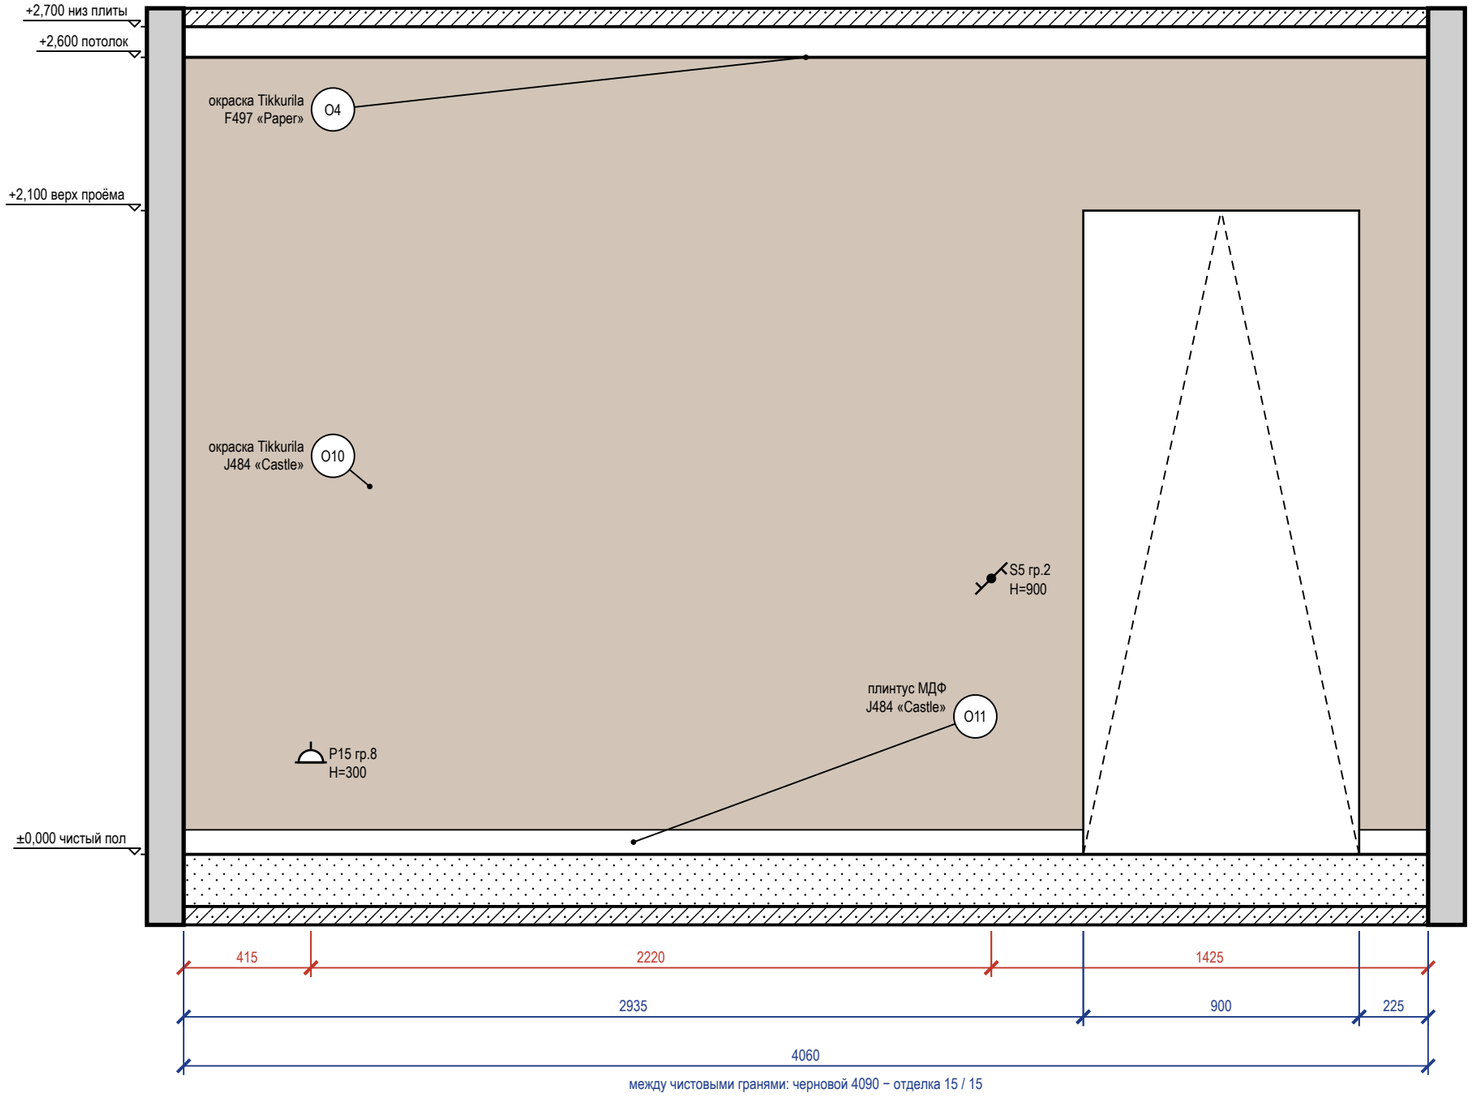


Схема развёрток (М 1:100)

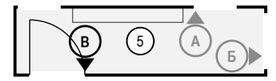


Ведомость отделки (на листе)

Марка	Поверхность	Материал, изделие	Цвет, код	Кол.
O4	потолок	окраска, Tikkurila Anti-Reflex 2, глубокоматовая, подготовка Q3	Tikkurila F497 «Paper»	4,5 м²
O10	стены	окраска, Tikkurila Optiva 20 Semimatt, шелковисто-матовая, подготовка К3	Tikkurila J484 «Castle»	8,7 м²
O11	плинтус	плинтус МДФ, h 80 мм, аналог: плинтус МДФ под окраску 80×16 мм, полуглянцевая	Tikkurila J484 «Castle»	3,2 м

6 **Плинтус МДФ 80×16 мм у окрашенной стены по керамограниту (плитке) (М 1:20)**

Узел 6 — лист С8

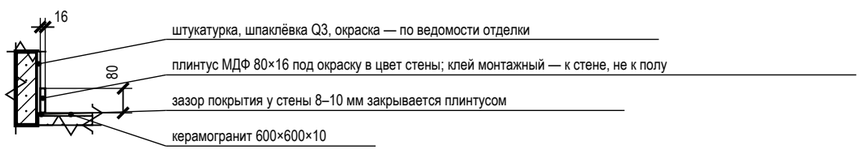

Примечания

1. Размеры — в мм от чистовых поверхностей стен; условные обозначения и общие указания — лист 3.

	Лист	№ док.	Подпись	Дата
Дизайнер	Кырлан А.С.			04.11.26

Проект: Четырёхкомнатная квартира — **М 1:20**

Развёртка стены В. Коридор (пом. 5)

Стадия	Лист	Листов
П	68	120

Развёртка стены А


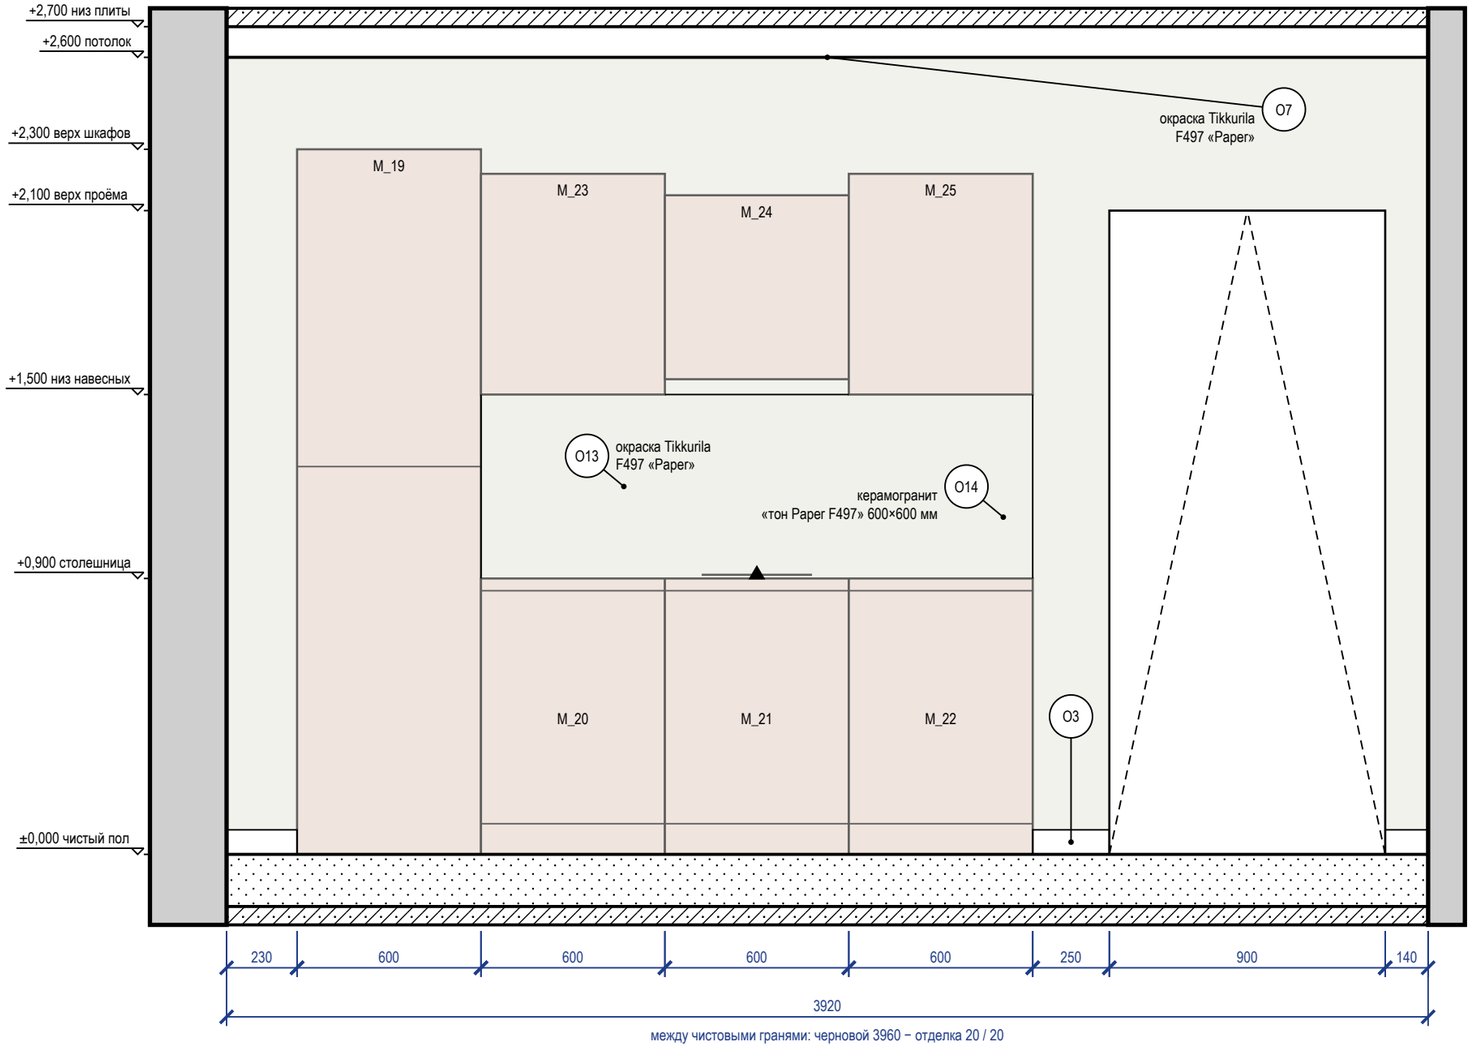


Схема развёрток (М 1:100)

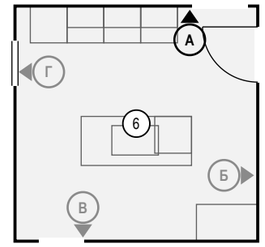

Ведомость отделки (на листе)

Марка	Поверхность	Материал, изделие	Цвет, код	Кол.
О3	плинтус	плинтус МДФ, h 80 мм, аналог: плинтус МДФ под окраску 80×16 мм, полуглянцевая	Tikkurila F497 «Paper»	0,6 м
О7	потолок	окраска, Tikkurila Luja 7, матовая, подготовка Q3	Tikkurila F497 «Paper»	15,2 м²
О13	стены	окраска, Tikkurila Luja 7, шелковисто-матовая, подготовка К3	Tikkurila F497 «Paper»	7,2 м²
О14	фартук	керамогранит, 600×600×9 мм, аналог: керамогранит матовый, тон F497, затирка CG2WA	#F1F1EC «тон Paper F497»	1,1 м²

Примечания

1. Размеры — в мм от чистовых поверхностей стен; условные обозначения и общие указания — лист 3.
2. Стена А показана двумя видами: здесь — архитектурная развёртка (мебель, отделка, проёмы, высоты), электроточки и выводы ВК с привязками и таблицей — на листе 70 («Привязки»).

					Проект: Четырёхкомнатная квартира	М 1:20
	Лист	№ док.	Подпись	Дата		
Дизайнер	Кырлан А.С.			04.11.26	Развёртка стены А. Кухня (пом. 6), кухонный фронт	Стадия: П; Лист: 69; Листов: 120

Развёртка стены А: электроточки и выводы

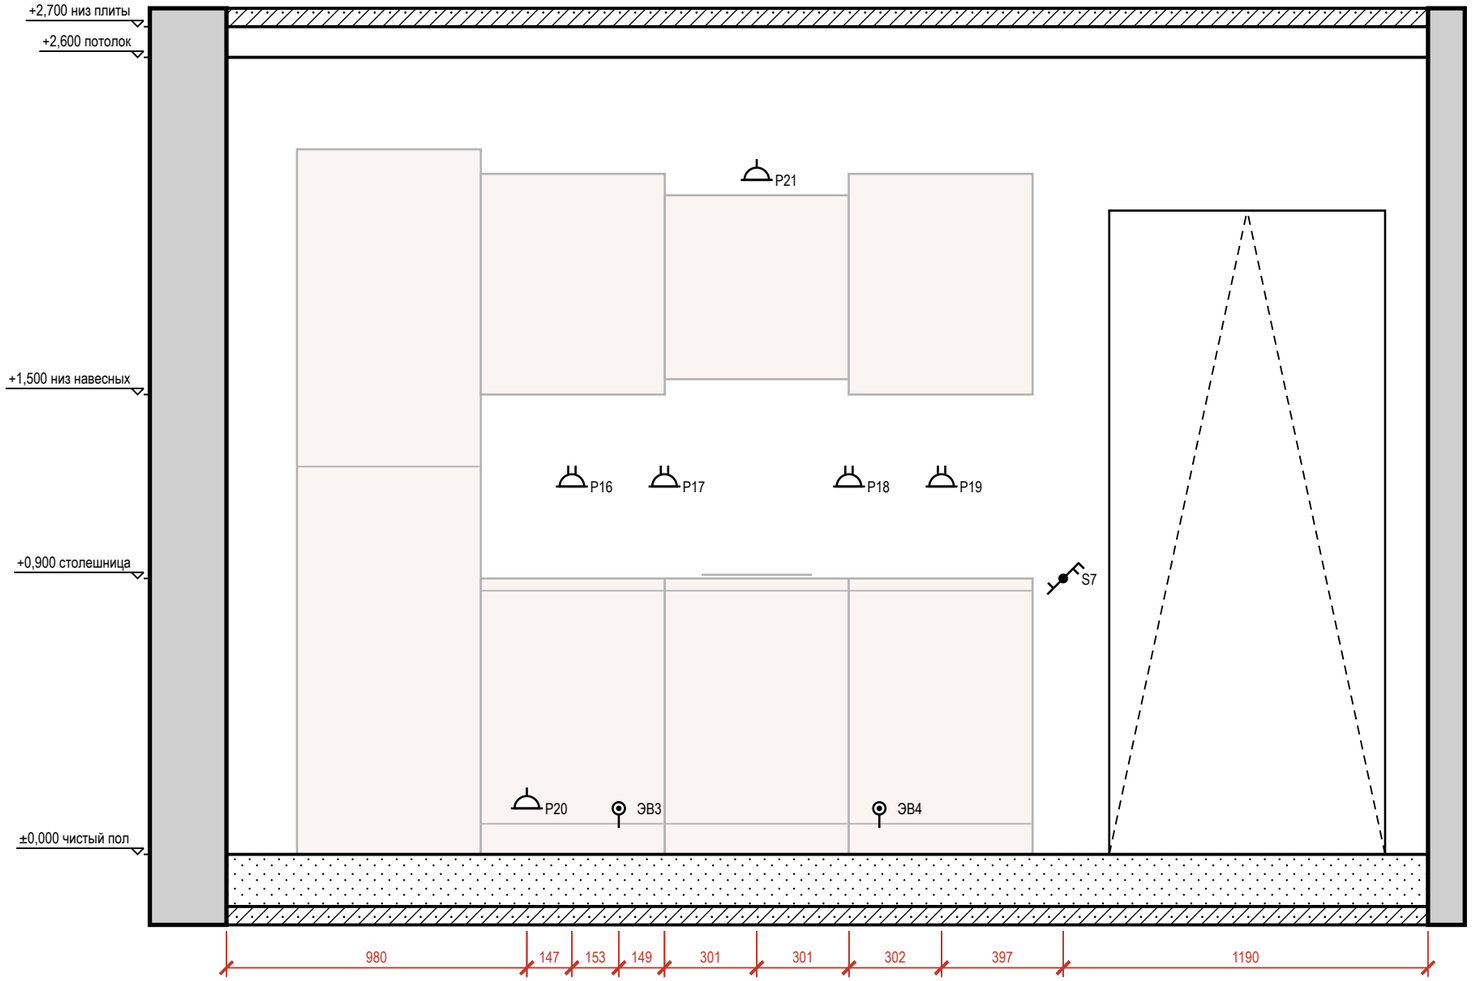



Таблица привязок электроточек и выводов

Марка	Назначение	От угла, мм	H от пола, мм	Примечание
P20	розетка: холодильник встроенный M_19 (розетка в модуле M_20)	980	150	гр. 10
P16	розетка: фартук: мелкая техника	1127	1200	рамка 2 поста, гр. 9
ЭВ3	вывод кабеля: варочная панель M_21	1280	150	гр. 11
P17	розетка: фартук: мелкая техника	1429	1200	рамка 2 поста, гр. 9
P21	розетка: вытяжка M_24 (в модуле, съёмная панель)	1730	2200	гр. 10
P18	розетка: фартук: мелкая техника	2031	1200	рамка 2 поста, гр. 9
ЭВ4	вывод кабеля: духовой шкаф M_21 (вывод в соседнем модуле M_22)	2130	150	гр. 12
P19	розетка: фартук: мелкая техника	2333	1200	рамка 2 поста, гр. 9
S7	выключатель	2730	900	гр. 1

Условные обозначения

- розетка с заземляющим контактом; у знака — марка, ×N постов в рамке, гр. — группа щита, H — высота оси, мм
- вывод кабеля для подключения прибора (без розетки), марка ЭВ
- выключатель одноклавишный
- выключатель двухклавишный (флажков — по числу клавиш)
- выключатель с проходной или перекрёстной клавишей (обратный флажок); тип клавиши — в подписи
- привязки точек и выводов от угла и от пола, мм
- марка развёртки: буква стены, стрелка — взгляд

Схема развёрток (М 1:100)

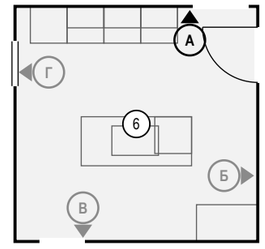

Примечания

1. Вид «Привязки» стены А — электроточки и выводы ВК; архитектурная развёртка (мебель, отделка, проёмы, высоты) — на листе 69. Мебель и приборы — подложкой для ориентира; их марки и обозначения мебели, проёмов и стен — там же.
2. Привязки — в мм: по горизонтали от левого чистового угла стены до оси изделия, H — от чистого пола до оси; все точки — в таблице привязок. Красная цепочка — привязки по осям; точки ближе 120 мм одна к другой в цепочку не дробятся — их привязки только в таблице.
3. У знака — марка электроточки (P — розетка, S — выключатель, Св — светильник, ЭВ — вывод кабеля); условные обозначения и общие указания — лист 3.

					Проект: Четырёхкомнатная квартира	М 1:20
	Лист	№ док.	Подпись	Дата	Привязки электроточек, стена А. Кухня (пом. 6)	Стадия / Лист / Листов
Дизайнер	Кырлан А.С.			04.11.26		П / 70 / 120

Развёртка стены Б


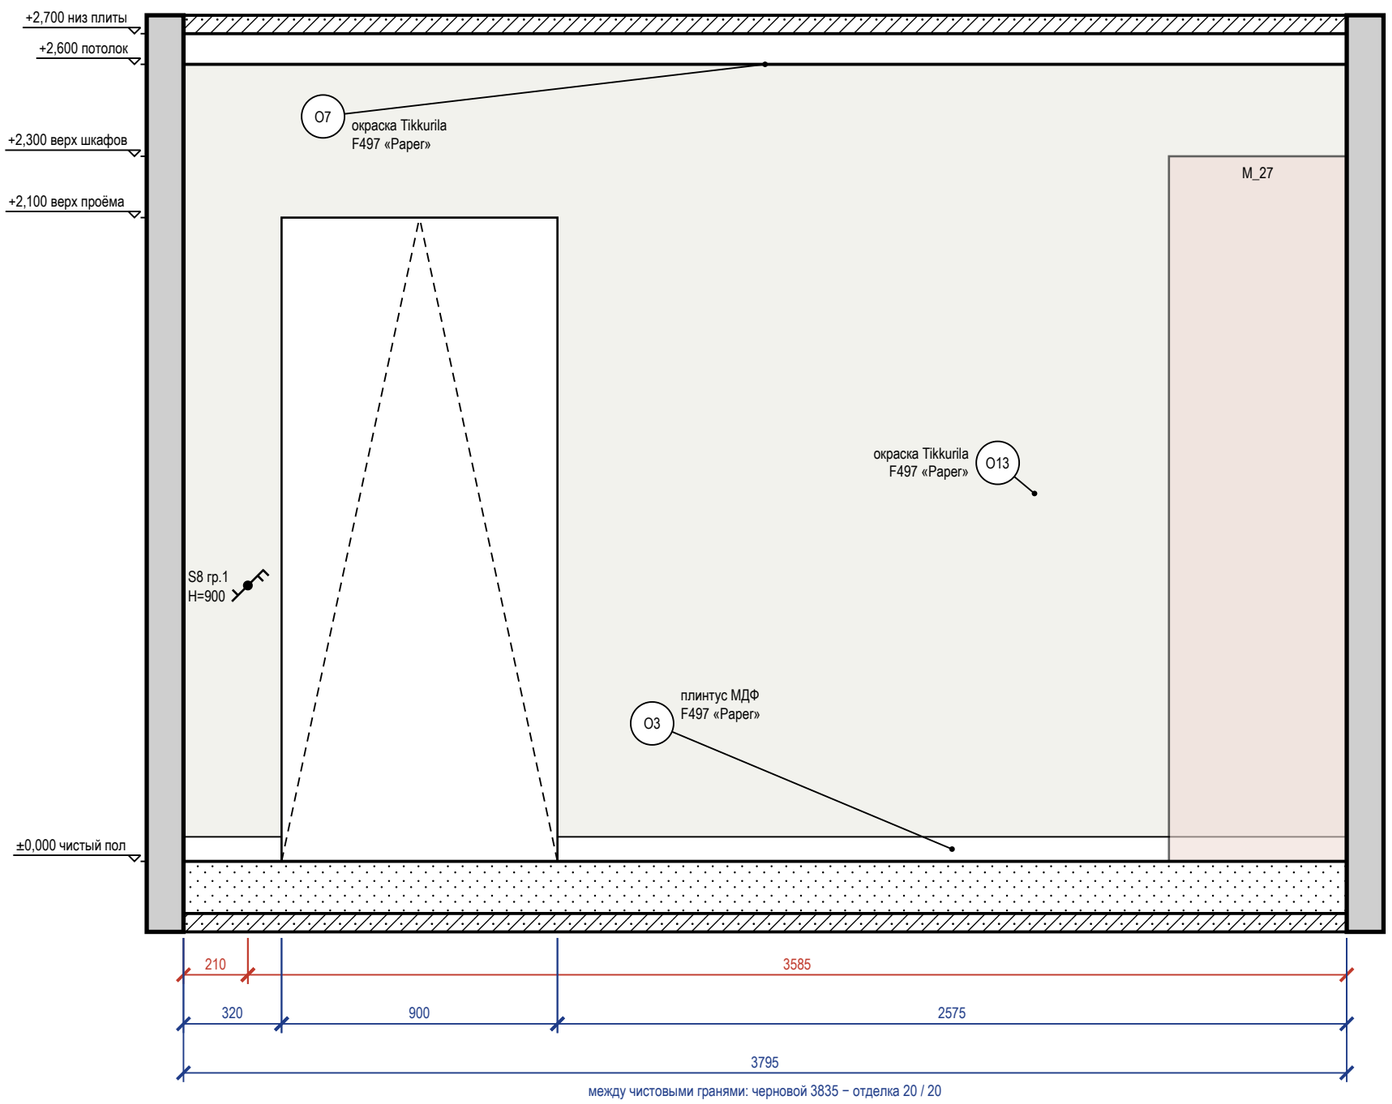


Схема развёрток (М 1:100)

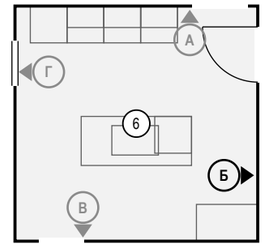

Ведомость отделки (на листе)

Марка	Поверхность	Материал, изделие	Цвет, код	Кол.
О3	плинтус	плинтус МДФ, h 80 мм, аналог: плинтус МДФ под окраску 80×16 мм, полуглянцевая	Tikkurila F497 «Paper»	2,9 м
О7	потолок	окраска, Tikkurila Luja 7, матовая, подготовка Q3	Tikkurila F497 «Paper»	15,2 м²
О13	стены	окраска, Tikkurila Luja 7, шелковисто-матовая, подготовка К3	Tikkurila F497 «Paper»	8 м²

Примечания

1. Размеры — в мм от чистовых поверхностей стен; условные обозначения и общие указания — лист 3.

					Проект: Четырёхкомнатная квартира		М 1:20
	Лист	№ док.	Подпись	Дата	Развёртка стены Б. Кухня (пом. 6)	Стадия	Лист	Листов
Дизайнер	Кырлан А.С.			04.11.26		П	71	120

Развёртка стены В


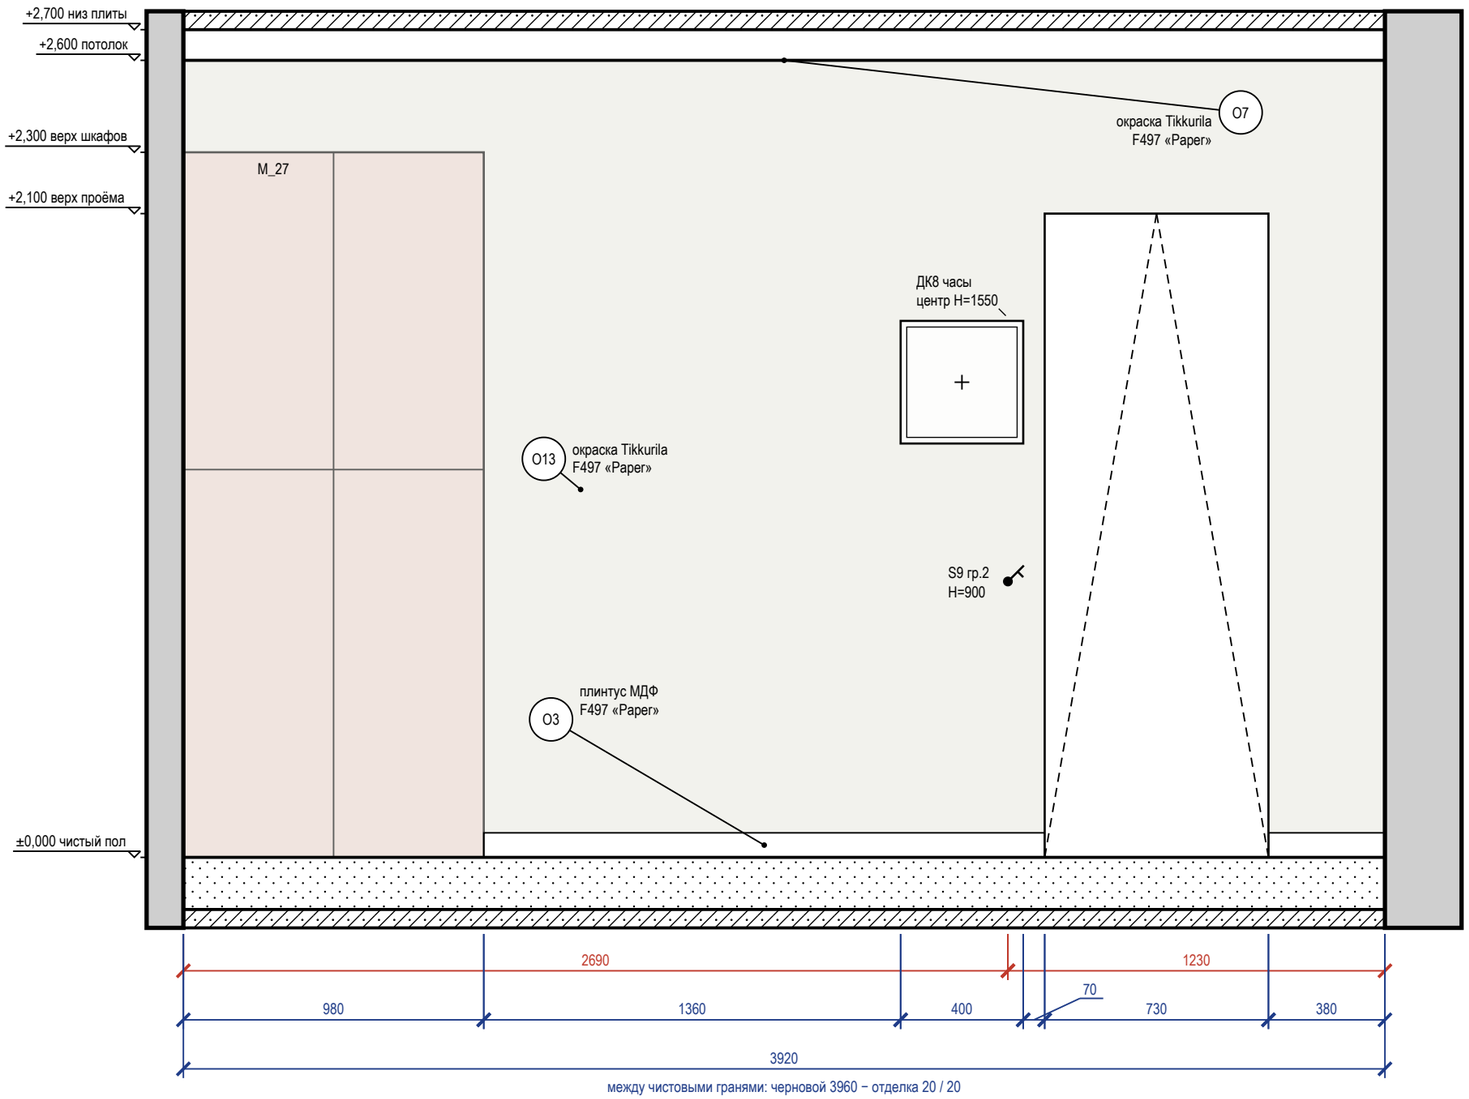


Схема развёрток (М 1:100)

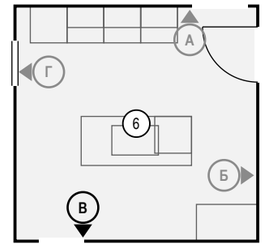

Ведомость отделки (на листе)

Марка	Поверхность	Материал, изделие	Цвет, код	Кол.
О3	плинтус	плинтус МДФ, h 80 мм, аналог: плинтус МДФ под окраску 80×16 мм, полуглянцевая	Tikkurila F497 «Paper»	2,2 м
О7	потолок	окраска, Tikkurila Luja 7, матовая, подготовка Q3	Tikkurila F497 «Paper»	15,2 м²
О13	стены	окраска, Tikkurila Luja 7, шелковисто-матовая, подготовка К3	Tikkurila F497 «Paper»	8,7 м²

Примечания

1. Размеры — в мм от чистовых поверхностей стен; условные обозначения и общие указания — лист 3.
2. Картины и зеркала крепить к основанию по паспорту изделия (закладные и анкеры — в перечне скрытых работ); крест — ось центра предмета.

					Проект: Четырёхкомнатная квартира	М 1:20
	Лист	№ док.	Подпись	Дата	Развёртка стены В. Кухня (пом. 6)	Стадия / Лист / Листов
Дизайнер	Кырлан А.С.			04.11.26		П / 72 / 120

Развёртка стены Г


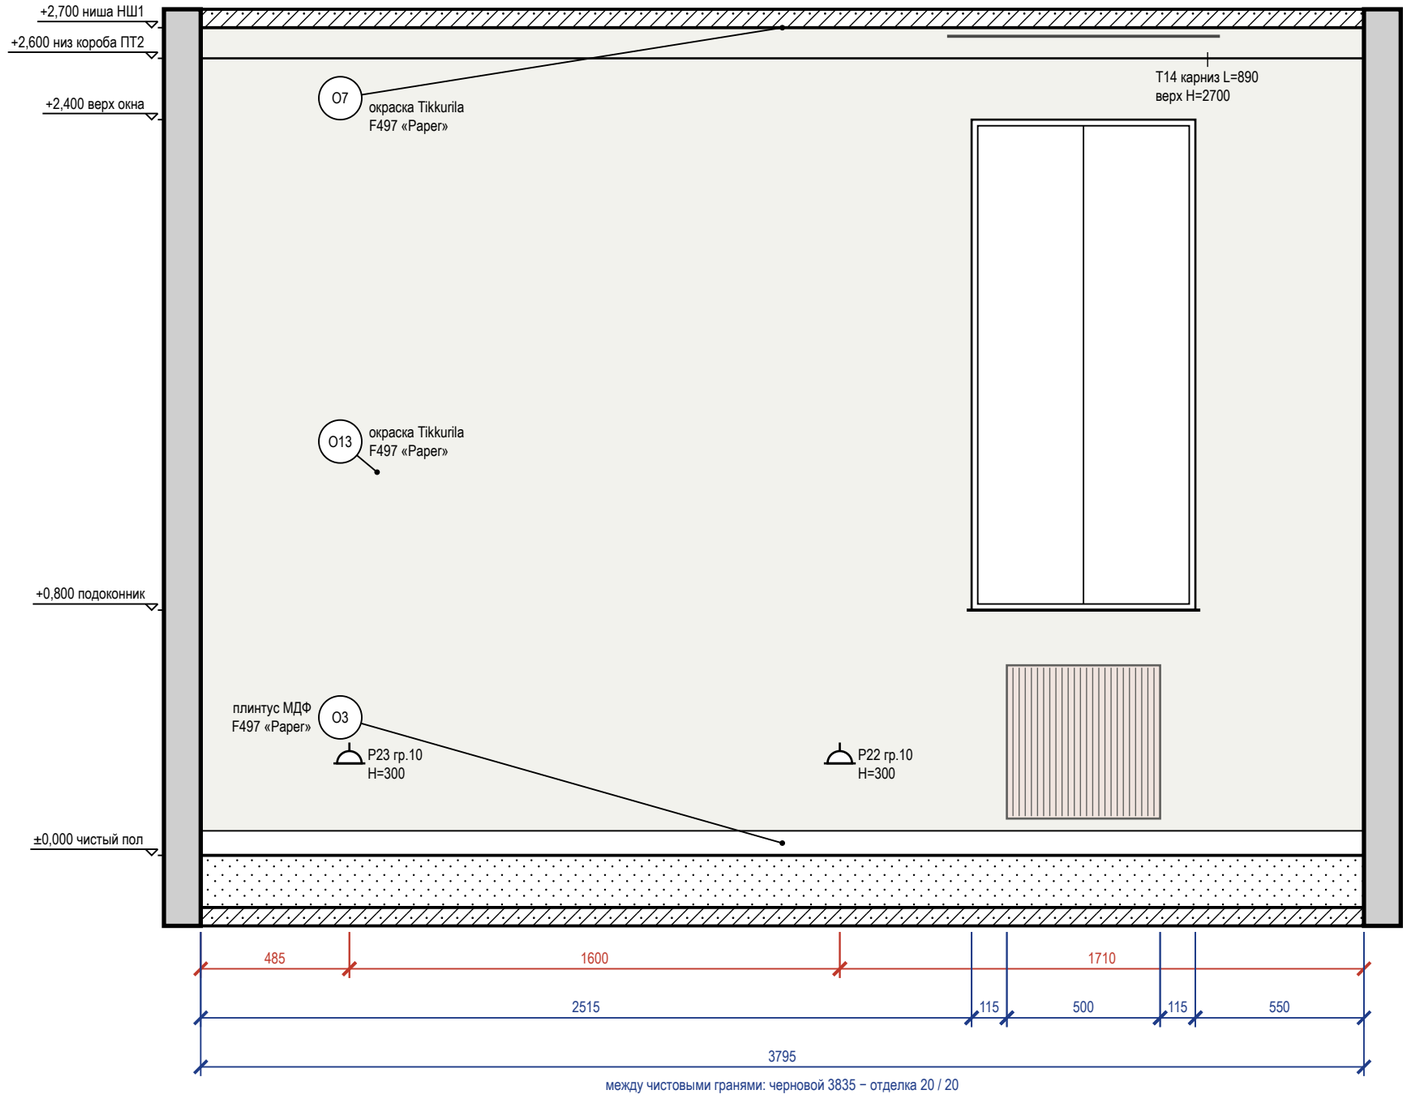


Схема развёрток (М 1:100)

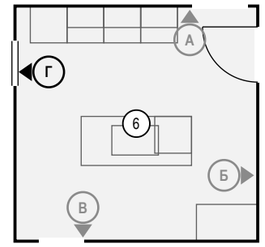

Ведомость отделки (на листе)


Марка	Поверхность	Материал, изделие	Цвет, код	Кол.
О3	плинтус	плинтус МДФ, h 80 мм, аналог: плинтус МДФ под окраску 80×16 мм, полуглянцевая	Tikkurila F497 «Paper»	3,8 м
О7	потолок	окраска, Tikkurila Luja 7, матовая, подготовка Q3	Tikkurila F497 «Paper»	15,2 м²
О13	стены	окраска, Tikkurila Luja 7, шелковисто-матовая, подготовка К3	Tikkurila F497 «Paper»	9,1 м²

Примечания

1. Размеры — в мм от чистовых поверхностей стен; условные обозначения и общие указания — лист 3.
2. Карнизы (шины) — по ведомости текстиля декоратора: длина L и верх H на развёртке — те же числа, что в ведомости; крепление — до окраски потолка.


					Проект: Четырёхкомнатная квартира	М 1:20
	Лист	№ док.	Подпись	Дата	Развёртка стены Г. Кухня (пом. 6)	Стадия / Лист / Листов
Дизайнер	Кырлан А.С.			04.11.26		П / 73 / 120

Развёртка стены А

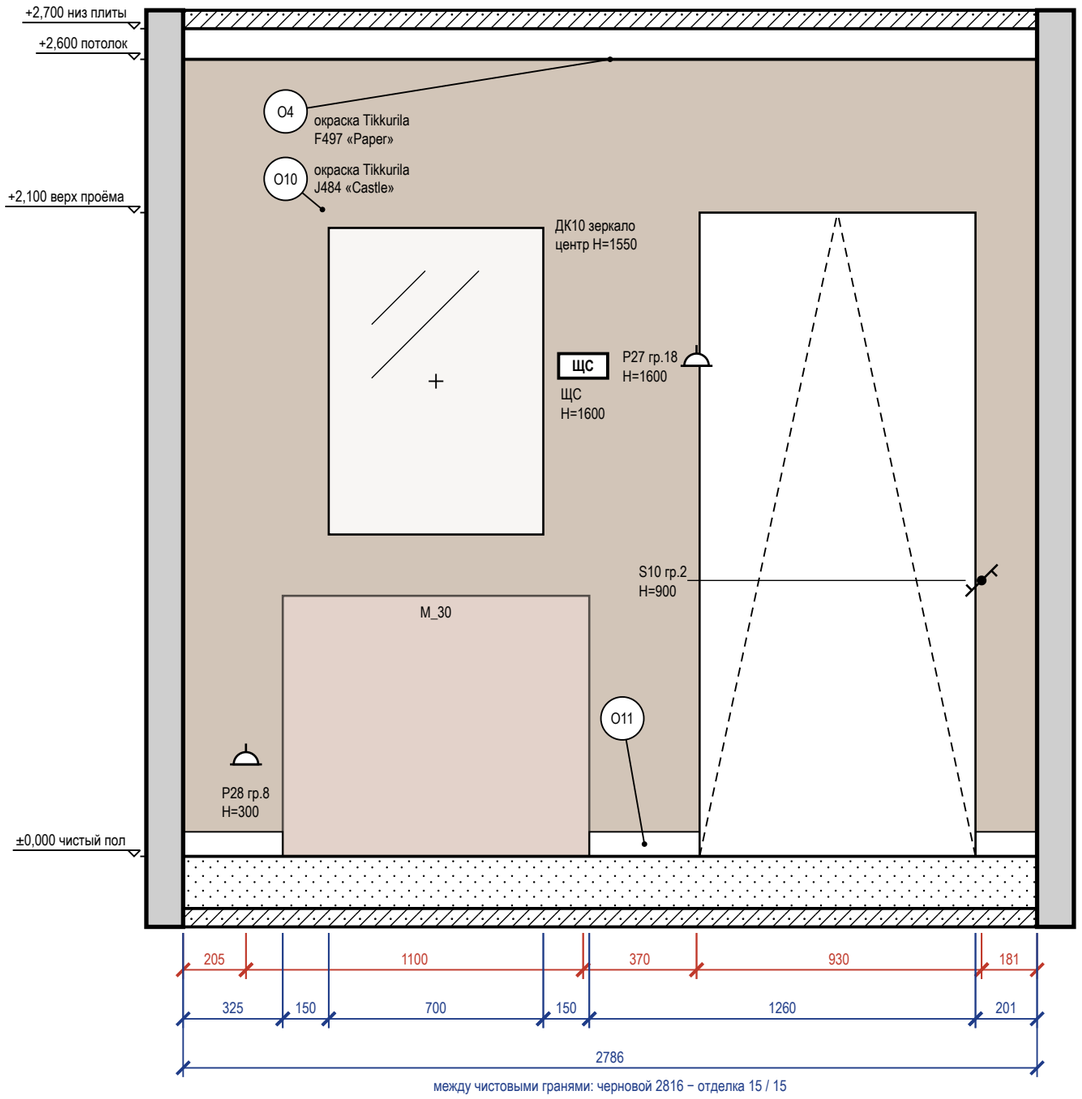


между чистовыми гранями: черновой 2816 − отделка 15 / 15

Развёртка стены Б

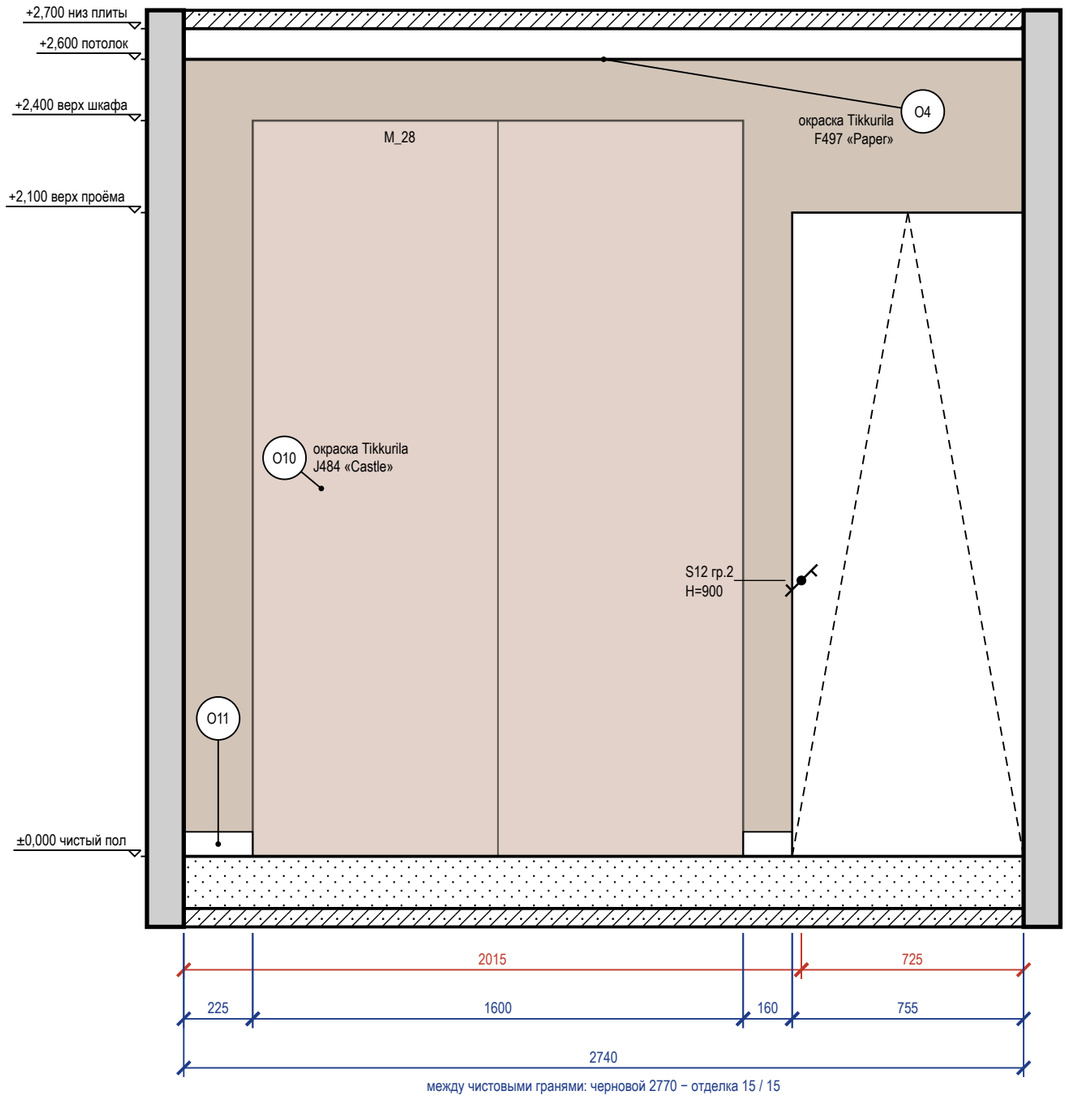

между чистовыми гранями: черновой 2770 − отделка 15 / 15

Схема развёрток (М 1:100)

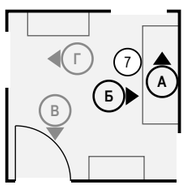

Ведомость отделки (на листе)


Марка	Поверхность	Материал, изделие	Цвет, код	Кол.
О4	потолок	окраска, Tikkurila Anti-Reflex 2, глубокоматовая, подготовка Q3	Tikkurila F497 «Paper»	7,8 м²
О10	стены	окраска, Tikkurila Optiva 20 Semimatt, шелковисто-матовая, подготовка К3	Tikkurila J484 «Castle»	10,9 м²
О11	плинтус	плинтус МДФ, h 80 мм, аналог: плинтус МДФ под окраску 80×16 мм, полуглянцевая	Tikkurila J484 «Castle»	1,3 м

Примечания

1. Размеры — в мм от чистовых поверхностей стен; условные обозначения и общие указания — лист 3.
2. Картины и зеркала крепить к основанию по паспорту изделия (закладные и анкеры — в перечне скрытых работ); крест — ось центра предмета.
3. Дверь заходит за угол помещения: на развёртке показана видимая часть проёма 770 из 900 мм — проверить привязку двери в модели.


					Проект: Четырёхкомнатная квартира — М 1:20
	Лист	№ док.	Подпись	Дата	Развёртки стен А, Б. Прихожая-коридор (пом. 7)
Дизайнер	Кырлан А.С.			04.11.26	Стадия: П; Лист: 74; Листов: 120

Развёртка стены В

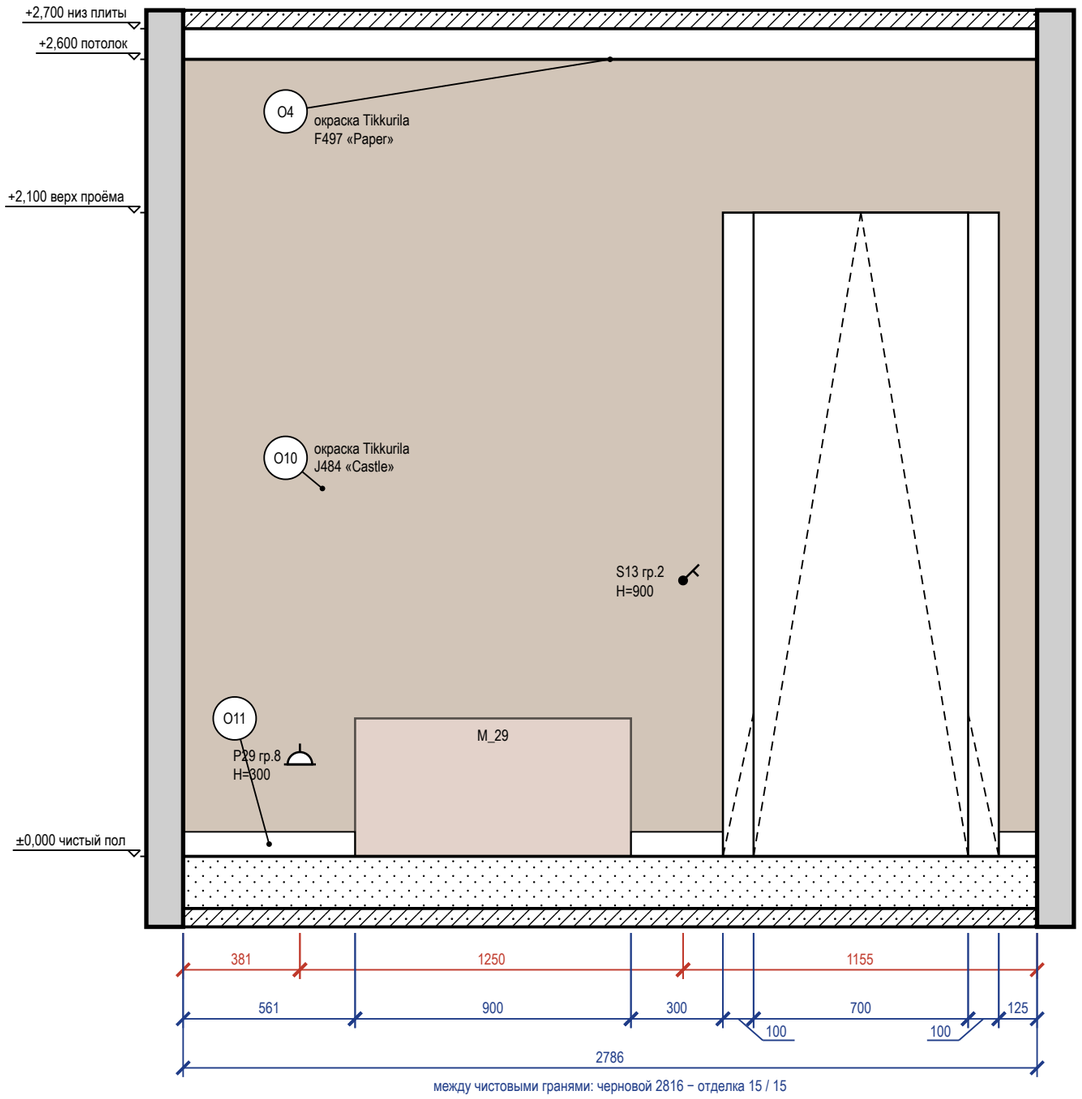


между чистовыми гранями: черновой 2816 − отделка 15 / 15

Развёртка стены Г

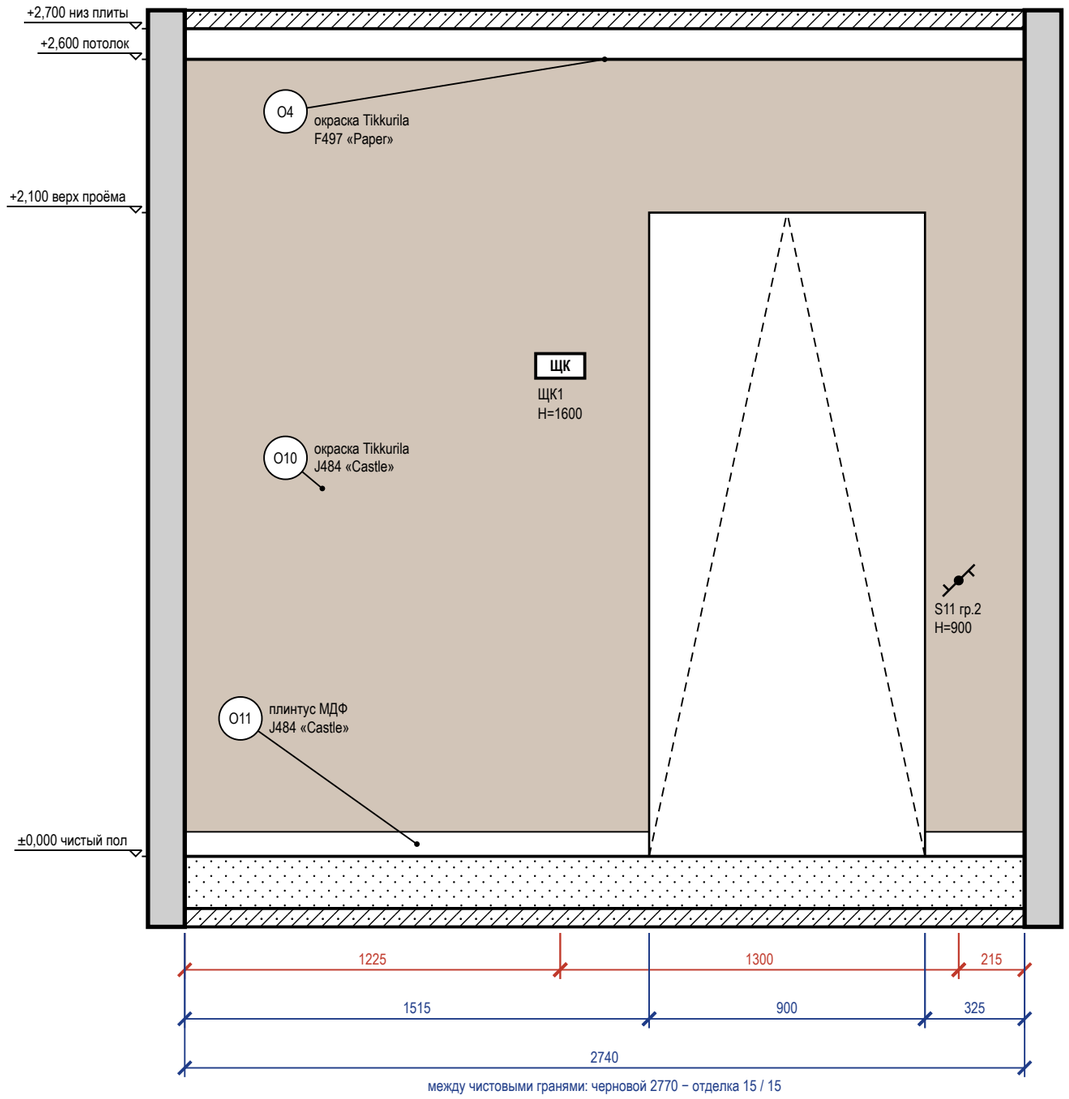

между чистовыми гранями: черновой 2770 − отделка 15 / 15

Схема развёрток (М 1:100)

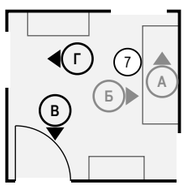

Ведомость отделки (на листе)

Марка	Поверхность	Материал, изделие	Цвет, код	Кол.
O4	потолок	окраска, Tikkurila Anti-Reflex 2, глубокоматовая, подготовка Q3	Tikkurila F497 «Paper»	7,8 м²
O10	стены	окраска, Tikkurila Optiva 20 Semimatt, шелковисто-матовая, подготовка К3	Tikkurila J484 «Castle»	9,1 м²
O11	плинтус	плинтус МДФ, h 80 мм, аналог: плинтус МДФ под окраску 80×16 мм, полуглянцевая	Tikkurila J484 «Castle»	2,8 м


Примечания

1. Размеры — в мм от чистовых поверхностей стен; условные обозначения и общие указания — лист 3.

					Проект: Четырёхкомнатная квартира — М 1:20
	Лист	№ док.	Подпись	Дата	Развёртки стен В, Г. Прихожая-коридор (пом. 7)
Дизайнер	Кырлан А.С.			04.11.26	


Стадия	Лист	Листов
П	75	120

Развёртка стены А

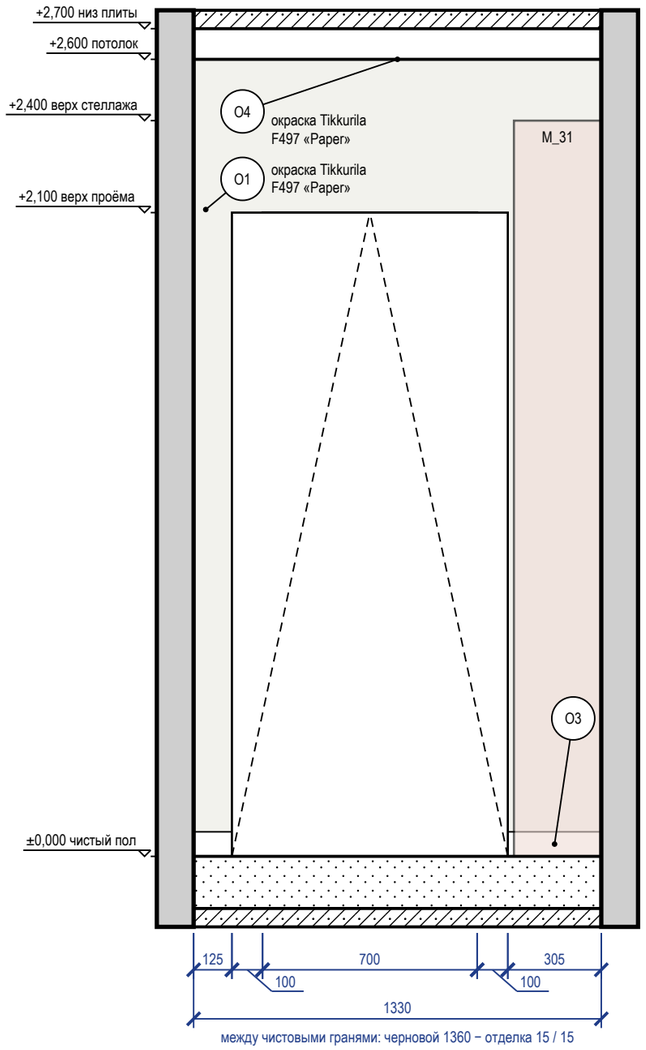


между чистовыми гранями: черновой 1360 − отделка 15 / 15

Развёртка стены Б

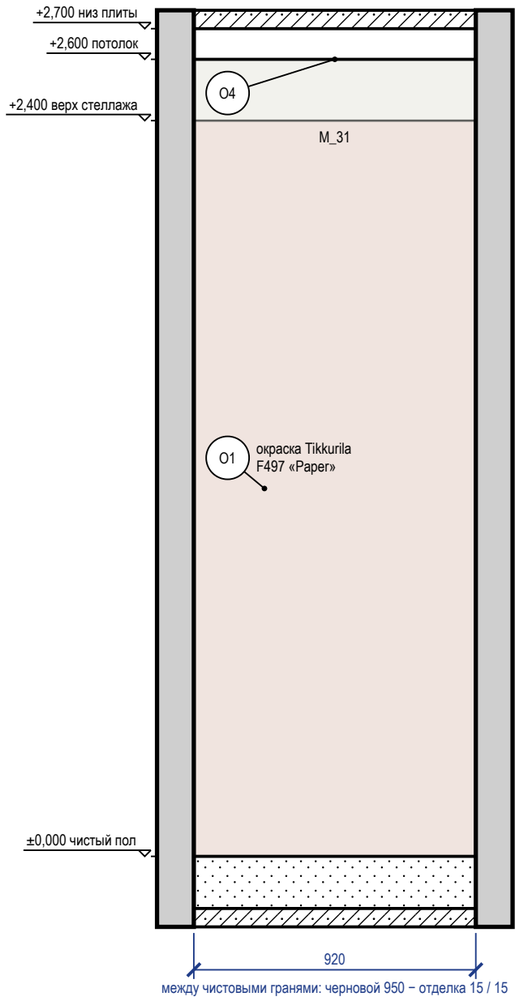

между чистовыми гранями: черновой 950 − отделка 15 / 15

Развёртка стены В

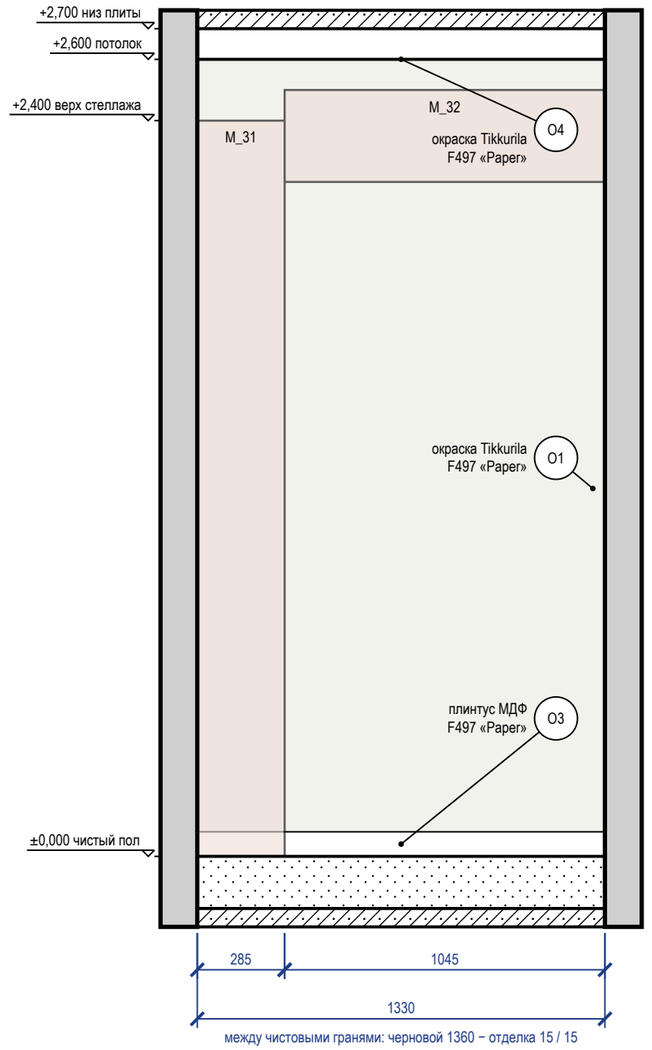

между чистовыми гранями: черновой 1360 − отделка 15 / 15

Схема развёрток (М 1:100)



Ведомость отделки (на листе)

Марка	Поверхность	Материал, изделие	Цвет, код	Кол.
O1	стены	окраска, Tikkurila Optiva 5 Matt, матовая, подготовка К3	Tikkurila F497 «Paper»	5,9 м²
O3	плинтус	плинтус МДФ, h 80 мм, аналог: плинтус МДФ под окраску 80×16 мм, полуглянцевая	Tikkurila F497 «Paper»	1,8 м
O4	потолок	окраска, Tikkurila Anti-Reflex 2, глубокоматовая, подготовка Q3	Tikkurila F497 «Paper»	1,3 м²

Примечания

1. Размеры — в мм от чистовых поверхностей стен; условные обозначения и общие указания — лист 3.

					Проект: Четырёхкомнатная квартира	М 1:20
	Лист	№ док.	Подпись	Дата	Развёртки стен А, Б, В. Гардеробная 2 (пом. 8)	Стадия / Лист / Листов
Дизайнер	Кырлан А.С.			04.11.26		П / 76 / 120

Развёртка стены Г


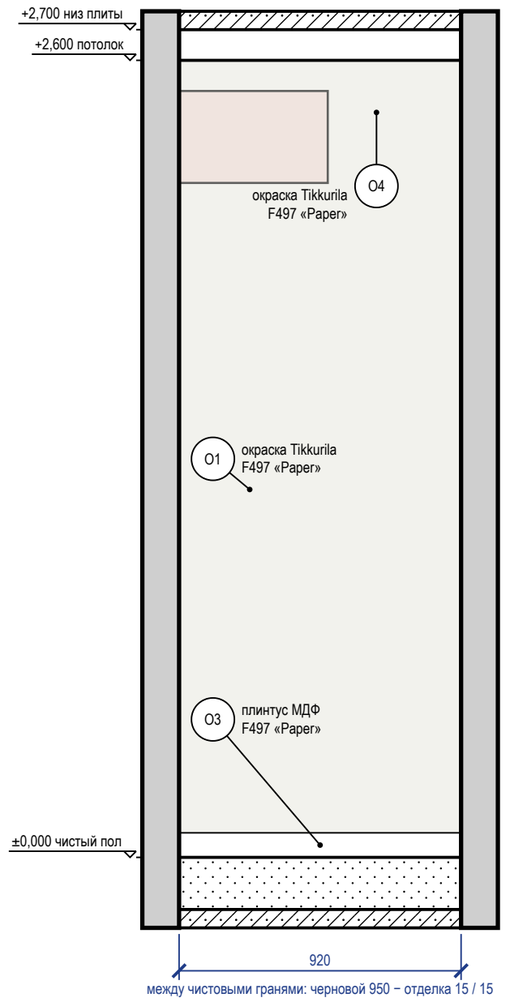


Схема развёрток (М 1:100)

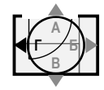

Ведомость отделки (на листе)

Марка	Поверхность	Материал, изделие	Цвет, код	Кол.
О1	стены	окраска, Tikkurila Optiva 5 Matt, матовая, подготовка К3	Tikkurila F497 «Paper»	2,4 м²
О3	плинтус	плинтус МДФ, h 80 мм, аналог: плинтус МДФ под окраску 80×16 мм, полуглянцевая	Tikkurila F497 «Paper»	0,9 м
О4	потолок	окраска, Tikkurila Anti-Reflex 2, глубокоматовая, подготовка Q3	Tikkurila F497 «Paper»	1,3 м²

Примечания

1. Размеры — в мм от чистовых поверхностей стен; условные обозначения и общие указания — лист 3.

					Проект: Четырёхкомнатная квартира — М 1:20
	Лист	№ док.	Подпись	Дата	
Дизайнер	Кырлан А.С.			04.11.26	Развёртка стены Г. Гардеробная 2 (пом. 8)
					Стадия: П; Лист: 77; Листов: 120

Развёртка стены А


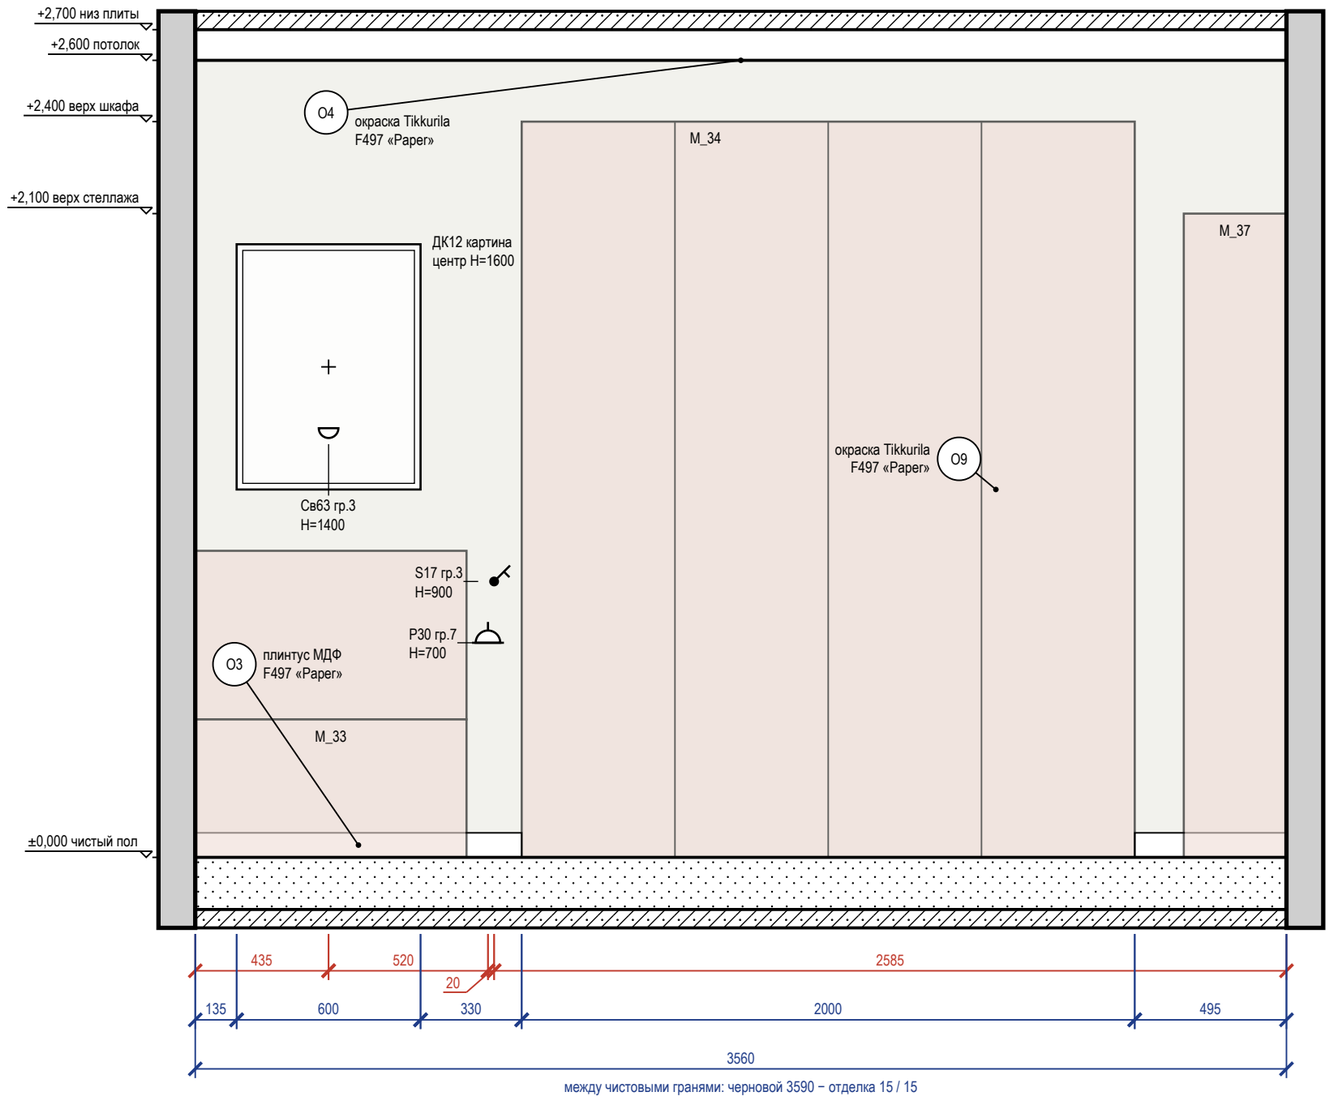


Схема развёрток (М 1:100)

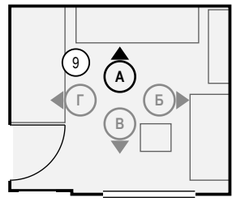

Ведомость отделки (на листе)

Марка	Поверхность	Материал, изделие	Цвет, код	Кол.
О3	плинтус	плинтус МДФ, h 80 мм, аналог: плинтус МДФ под окраску 80×16 мм, полуглянцевая	Tikkurila F497 «Paper»	1,6 м
О4	потолок	окраска, Tikkurila Anti-Reflex 2, глубокоматовая, подготовка Q3	Tikkurila F497 «Paper»	11 м²
О9	стены	окраска, Tikkurila Joker, шелковисто-матовая, подготовка К3	Tikkurila F497 «Paper»	9,3 м²

Примечания

1. Размеры — в мм от чистовых поверхностей стен; условные обозначения и общие указания — лист 3.
2. Картины и зеркала крепить к основанию по паспорту изделия (закладные и анкеры — в перечне скрытых работ); крест — ось центра предмета.

					Проект: Четырёхкомнатная квартира — М 1:20
	Лист	№ док.	Подпись	Дата	
Дизайнер	Кырлан А.С.			04.11.26	Развёртка стены А. Детская 2 (пом. 9)

Стадия	Лист	Листов
П	78	120

Развёртка стены Б


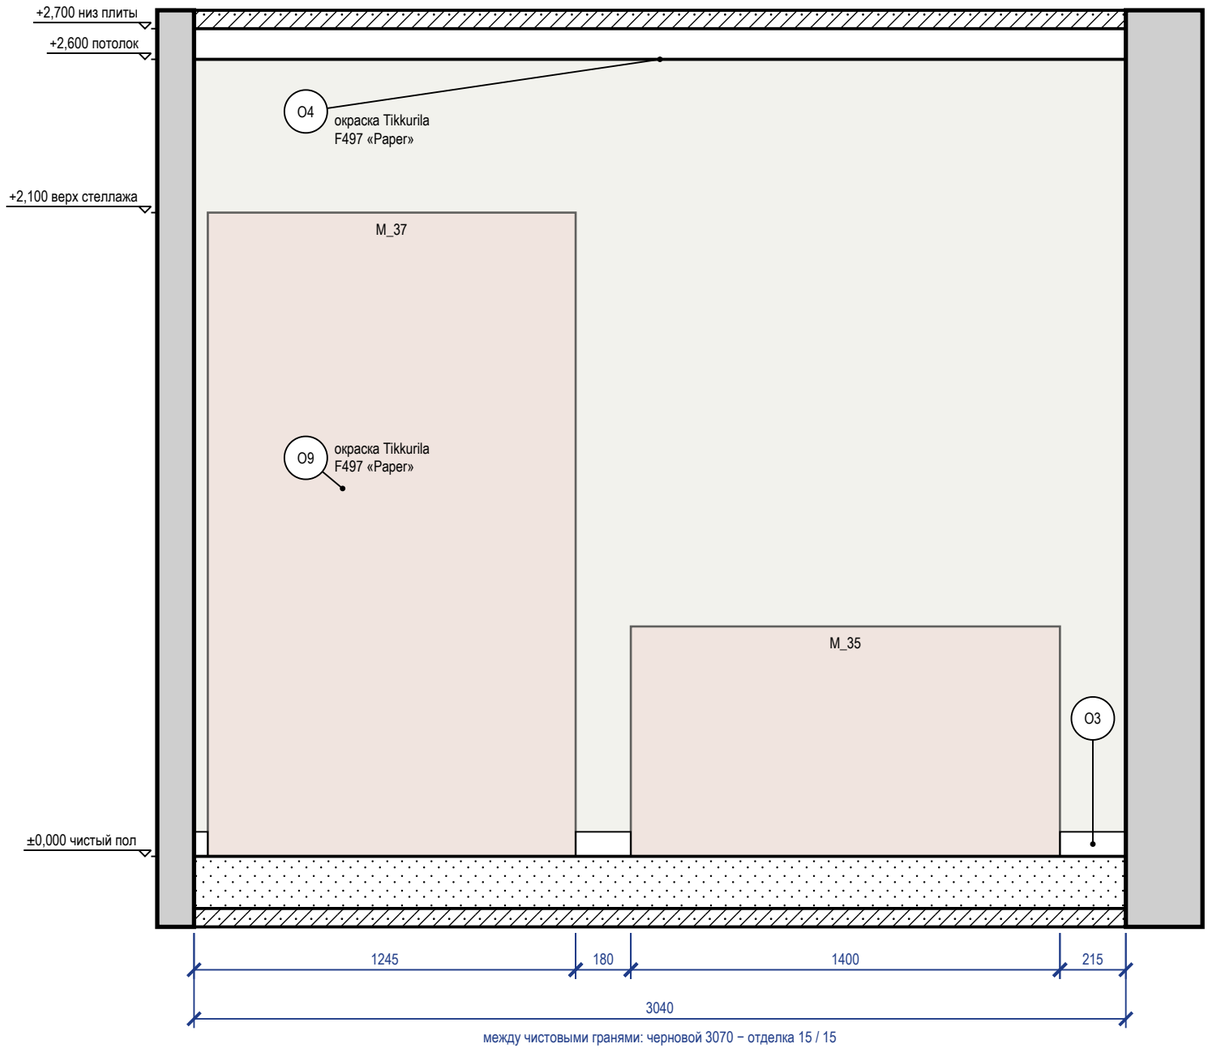


Схема развёрток (М 1:100)

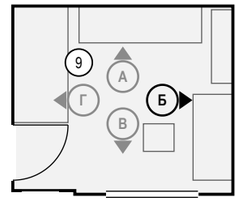

Ведомость отделки (на листе)

Марка	Поверхность	Материал, изделие	Цвет, код	Кол.
O3	плинтус	плинтус МДФ, h 80 мм, аналог: плинтус МДФ под окраску 80×16 мм, полуглянцевая	Tikkurila F497 «Paper»	0,4 м
O4	потолок	окраска, Tikkurila Anti-Reflex 2, глубокоматовая, подготовка Q3	Tikkurila F497 «Paper»	11 м²
O9	стены	окраска, Tikkurila Joker, шелковисто-матовая, подготовка К3	Tikkurila F497 «Paper»	7,9 м²

Примечания

1. Размеры — в мм от чистовых поверхностей стен; условные обозначения и общие указания — лист 3.
2. Стена Б показана двумя видами: здесь — архитектурная развёртка (мебель, отделка, проёмы, высоты), электроточки и выводы ВК с привязками и таблицей — на листе 80 («Привязки»).

					Проект: Четырёхкомнатная квартира — М 1:20
	Лист	№ док.	Подпись	Дата	Развёртка стены Б. Детская 2 (пом. 9)
Дизайнер	Кырлан А.С.			04.11.26	Стадия: П; Лист: 79; Листов: 120

Развёртка стены Б: электроточки и выводы

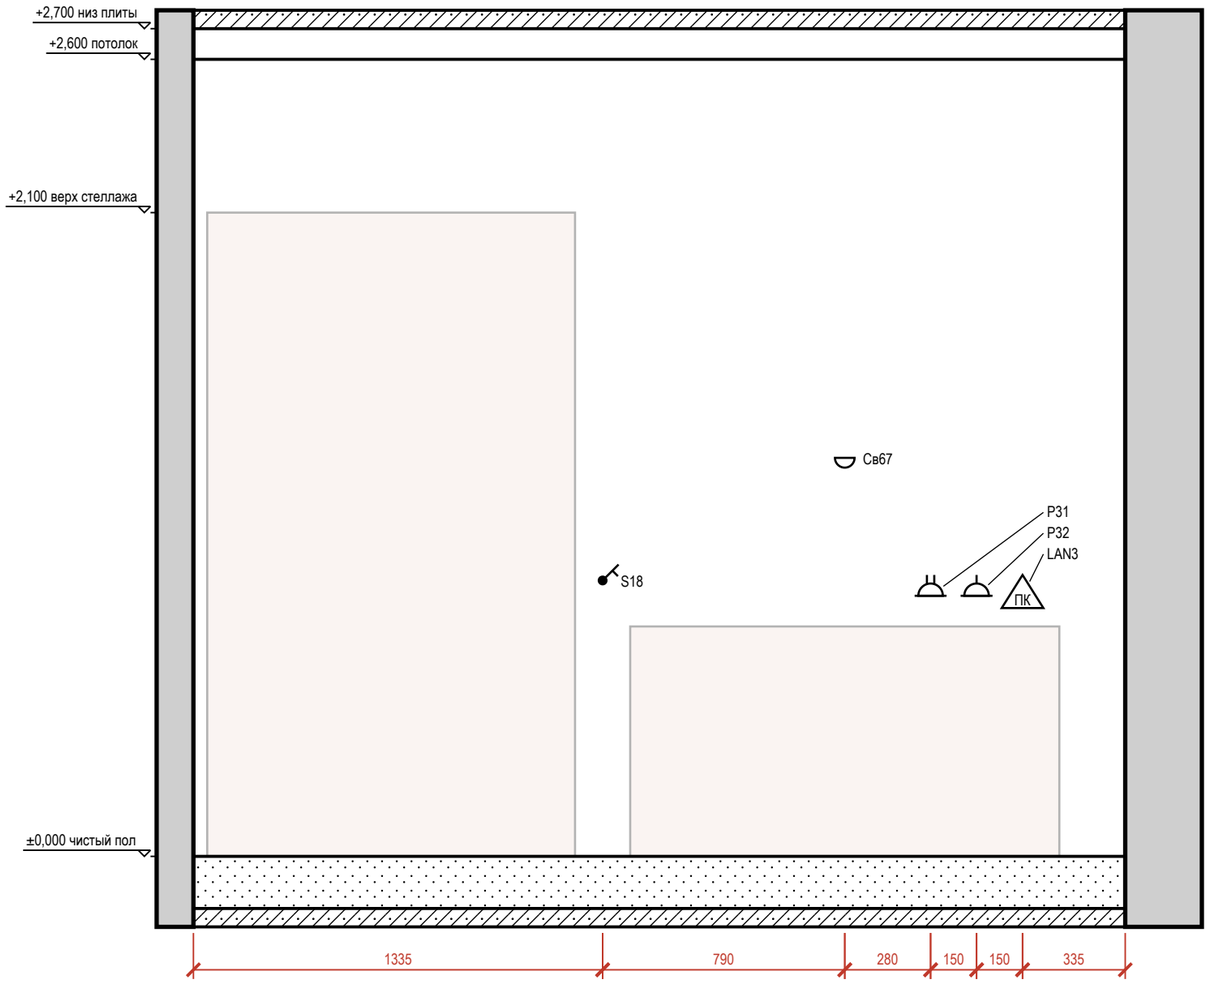



Таблица привязок электроточек и выводов

Марка	Назначение	От угла, мм	Н от пола, мм	Примечание
S18	выключатель	1335	900	гр. 3
Св67	светильник настенный	2125	1300	гр. 3
P31	розетка: рабочий стол М_35	2405	850	рамка 2 поста, гр. 7
P32	розетка: рабочий стол М_35	2555	850	гр. 7
LAN3	розетка RJ45: рабочий стол М_35	2705	850	

Условные обозначения

- розетка с заземляющим контактом; у знака — марка, ×N постов в рамке, гр. — группа щита, Н — высота оси, мм
- выключатель одноклавишный
- светильник настенный (бра), Н — высота оси
- ПК — розетка компьютерная RJ45
- привязки точек и выводов от угла и от пола, мм
- A — марка развёртки: буква стены, стрелка — взгляд

Схема развёрток (М 1:50)

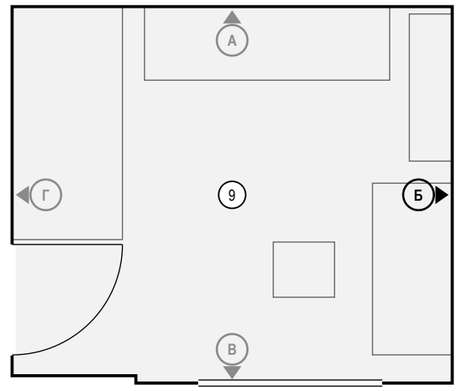

Примечания

1. Вид «Привязки» стены Б — электроточки и выводы ВК; архитектурная развёртка (мебель, отделка, проёмы, высоты) — на листе 79. Мебель и приборы — подложкой для ориентира; их марки и обозначения мебели, проёмов и стен — там же.
2. Привязки — в мм: по горизонтали от левого чистового угла стены до оси изделия, Н — от чистого пола до оси; все точки — в таблице привязок. Красная цепочка — привязки по осям; точки ближе 120 мм одна к другой в цепочку не дробятся — их привязки только в таблице.
3. У знака — марка электроточки (Р — розетка, S — выключатель, Св — светильник, ЭВ — вывод кабеля); условные обозначения и общие указания — лист 3.

					Проект: Четырёхкомнатная квартира	М 1:20
	Лист	№ док.	Подпись	Дата		
Дизайнер	Кырлан А.С.			04.11.26	Привязки электроточек, стена Б. Детская 2 (пом. 9)	Стадия: П; Лист: 80; Листов: 120

Развёртка стены В


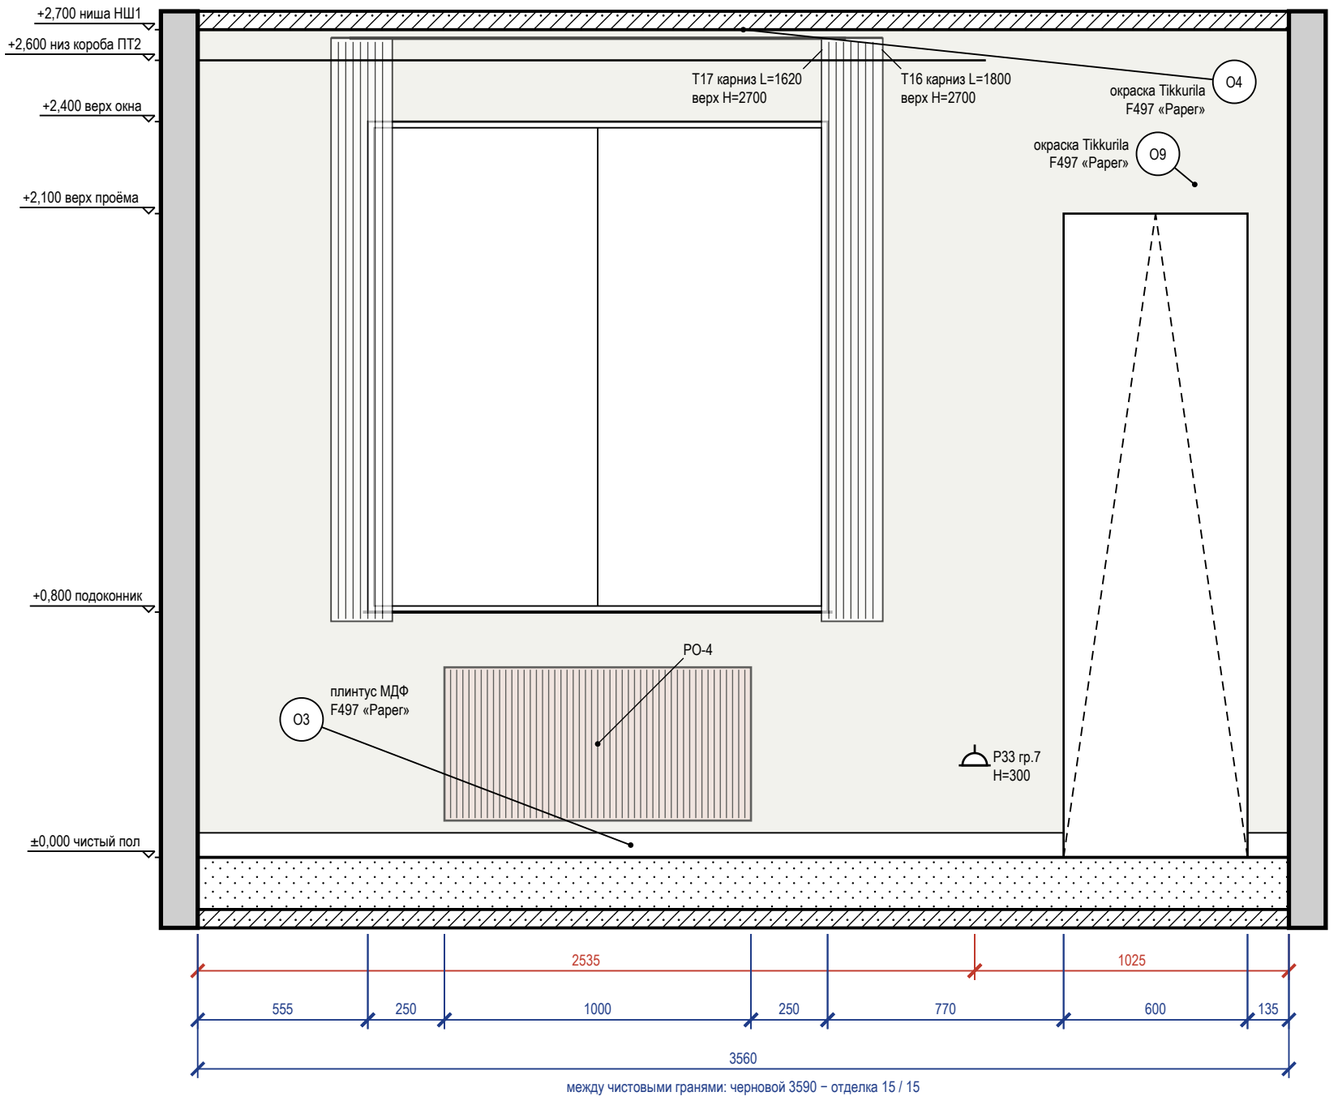


Схема развёрток (М 1:100)

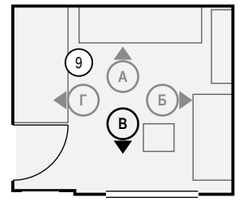

Ведомость отделки (на листе)

Марка	Поверхность	Материал, изделие	Цвет, код	Кол.
О3	плинтус	плинтус МДФ, h 80 мм, аналог: плинтус МДФ под окраску 80×16 мм, полуглянцевая	Tikkurila F497 «Paper»	3 м
О4	потолок	окраска, Tikkurila Anti-Reflex 2, глубокоматовая, подготовка Q3	Tikkurila F497 «Paper»	11 м²
О9	стены	окраска, Tikkurila Joker, шелковисто-матовая, подготовка К3	Tikkurila F497 «Paper»	6 м²

Примечания

1. Размеры — в мм от чистовых поверхностей стен; условные обозначения и общие указания — лист 3.
2. Карнизы (шины) — по ведомости текстиля декоратора: длина L и верх H на развёртке — те же числа, что в ведомости; крепление — до окраски потолка.

					Проект: Четырёхкомнатная квартира	М 1:20
	Лист	№ док.	Подпись	Дата		
Дизайнер	Кырлан А.С.			04.11.26	Развёртка стены В. Детская 2 (пом. 9)	

Стадия	Лист	Листов
П	81	120

Развёртка стены Г


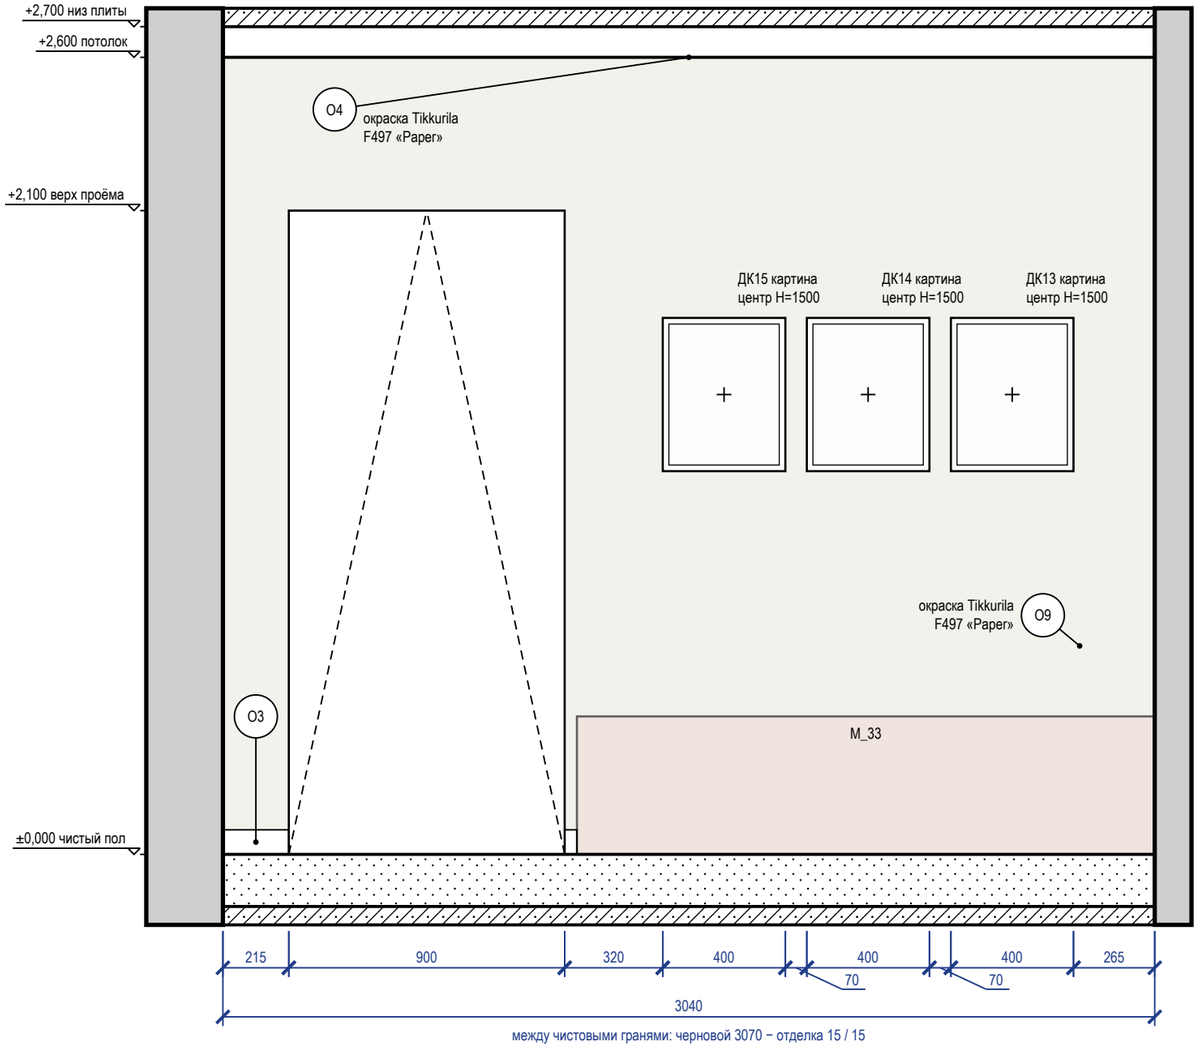


Схема развёрток (М 1:100)

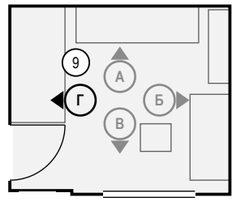

Ведомость отделки (на листе)


Марка	Поверхность	Материал, изделие	Цвет, код	Кол.
О3	плинтус	плинтус МДФ, h 80 мм, аналог: плинтус МДФ под окраску 80×16 мм, полуглянцевая	Tikkurila F497 «Paper»	0,3 м
О4	потолок	окраска, Tikkurila Anti-Reflex 2, глубокоматовая, подготовка Q3	Tikkurila F497 «Paper»	11 м²
О9	стены	окраска, Tikkurila Joker, шелковисто-матовая, подготовка К3	Tikkurila F497 «Paper»	6 м²

Примечания

1. Размеры — в мм от чистовых поверхностей стен; условные обозначения и общие указания — лист 3.
2. Картины и зеркала крепить к основанию по паспорту изделия (закладные и анкеры — в перечне скрытых работ); крест — ось центра предмета.


					Проект: Четырёхкомнатная квартира — М 1:20
	Лист	№ док.	Подпись	Дата	Развёртка стены Г. Детская 2 (пом. 9)
Дизайнер	Кырлан А.С.			04.11.26	Стадия: П; Лист: 82; Листов: 120

Развёртка стены А

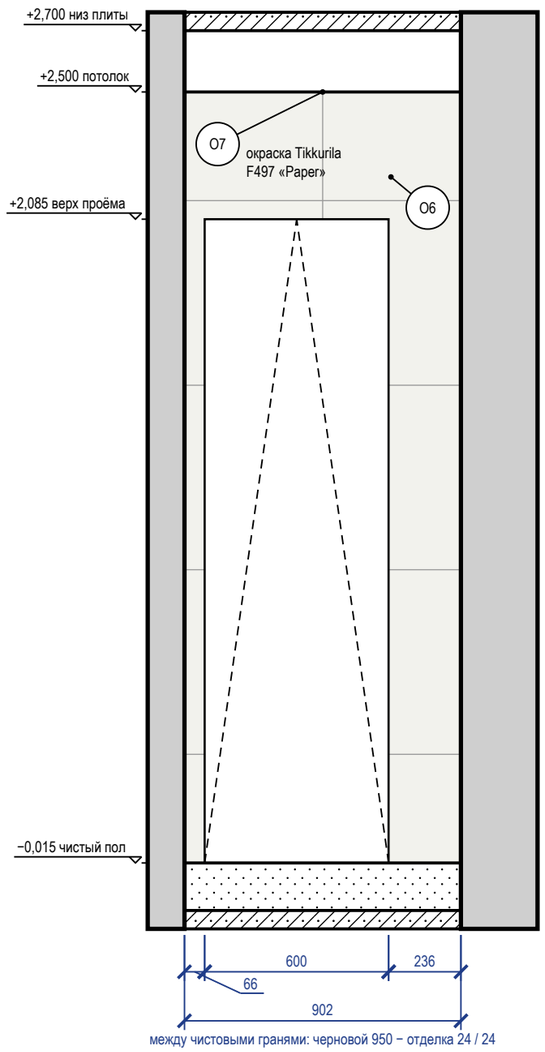


между чистовыми гранями: черновой 950 − отделка 24 / 24

Развёртка стены Б

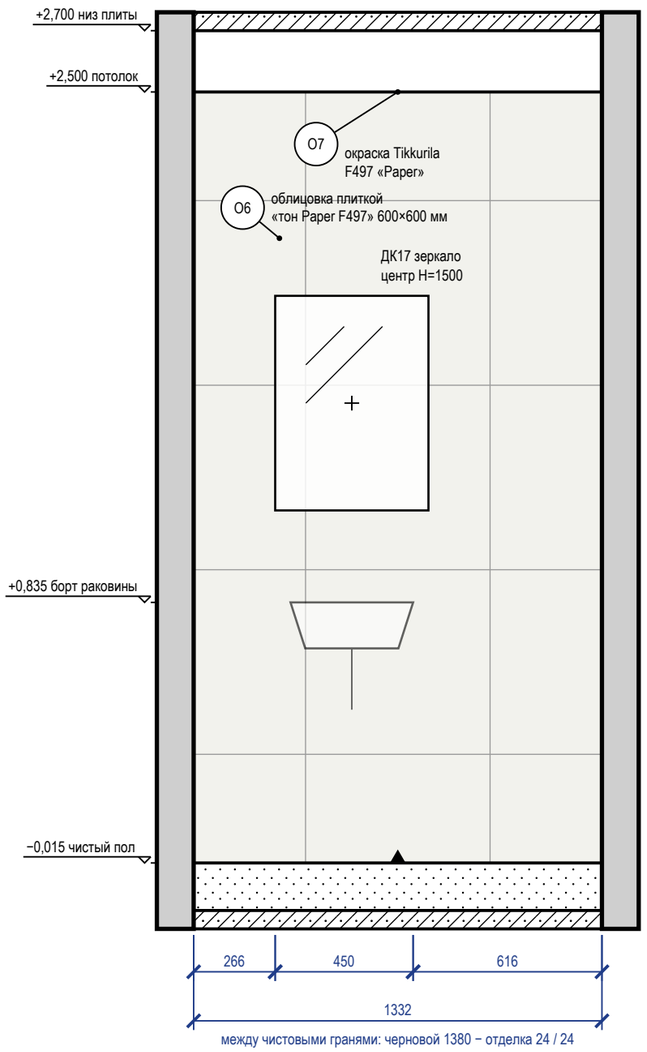


между чистовыми гранями: черновой 1380 − отделка 24 / 24

Развёртка стены В

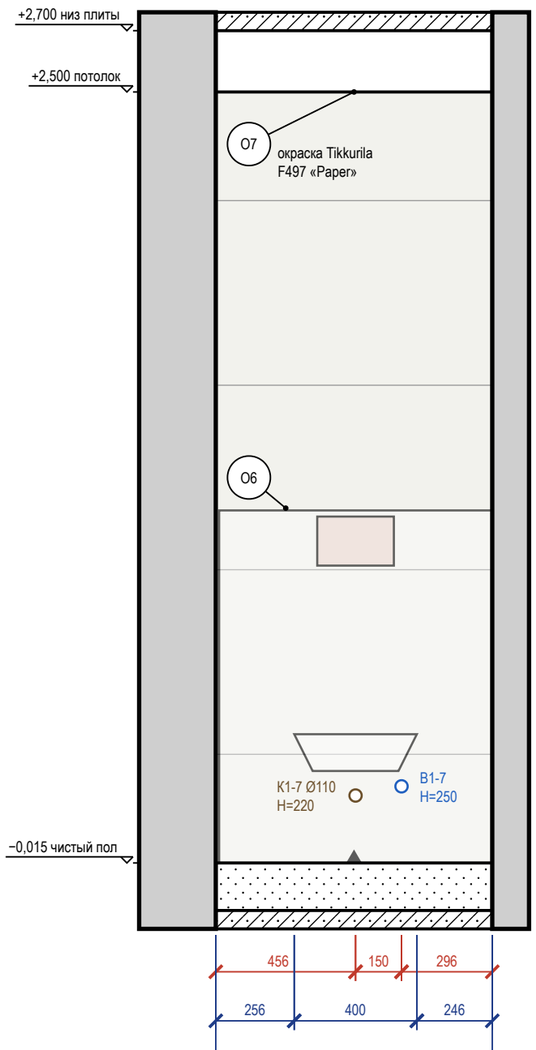

между чистовыми гранями: черновой 950 − отделка 24 / 24

Схема развёрток (М 1:100)

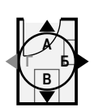

Ведомость отделки (на листе)

Марка	Поверхность	Материал, изделие	Цвет, код	Кол.
О6	стены	облицовка плиткой, 600×600×9 мм, аналог: керамогранит матовый, тон F497, затирка CG2WA	#F1F1EC «тон Paper F497»	6,6 м²
О7	потолок	окраска, Tikkurila Luja 7, матовая, подготовка Q3	Tikkurila F497 «Paper»	1,3 м²

Примечания

1. Размеры — в мм от чистовых поверхностей стен; условные обозначения и общие указания — лист 3.
2. Стена Б показана двумя видами: здесь — архитектурная развёртка (мебель, отделка, проёмы, высоты), электроточки и выводы ВК с привязками и таблицей — на листе 84 («Привязки»).
3. Облицовка — по сетке швов 2 мм, раскладка от оси стены (треугольник у пола), по высоте — от середины облицовки, подрезки у пола и у потолка поровну; подрезки — по листу раскладки плитки.
4. Гидроизоляция в 2 слоя, заход на стены 200 мм — до облицовки, с актом скрытых работ и тестом проливом (узел — на листе узлов).
5. Картины и зеркала крепить к основанию по паспорту изделия (закладные и анкеры — в перечне скрытых работ); крест — ось центра предмета.

					Проект: Четырёхкомнатная квартира — М 1:20
	Лист	№ док.	Подпись	Дата	
Дизайнер	Кырлан А.С.			04.11.26	Развёртки стен А, Б, В. Санузел (пом. 10)

Стадия	Лист	Листов
П	83	120

Развёртка стены Б: электроточки и выводы

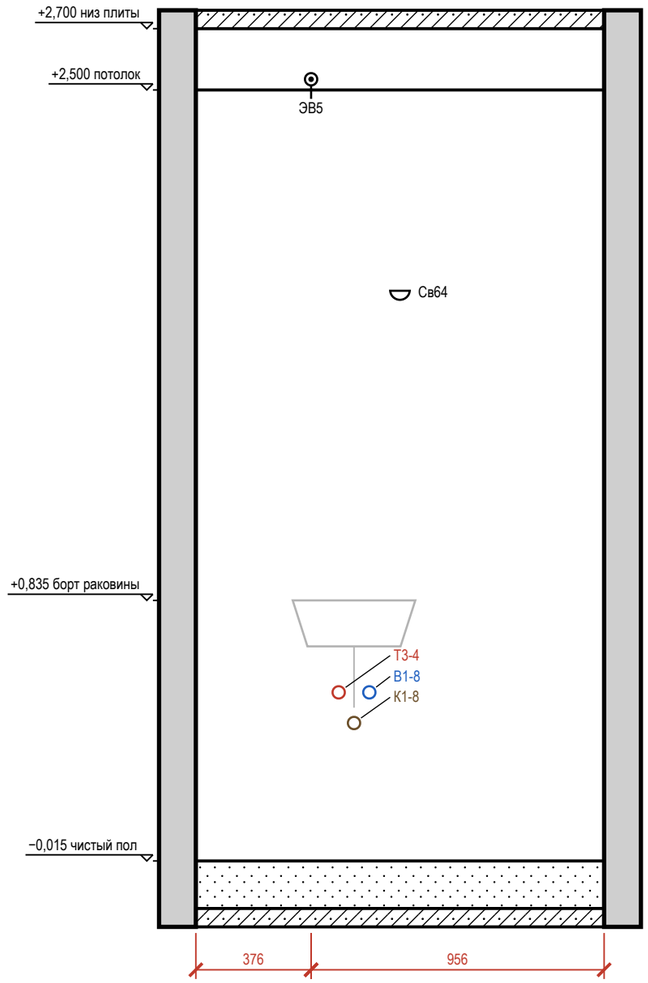



Таблица привязок электроточек и выводов

Марка	Назначение	От угла, мм	Н от пола, мм	Примечание
ЭВ5	вывод кабеля: вентилятор ВР3 (таймер выбега)	376	2550	гр. 4
Т3-4	горячая вода — умывальник	466	550	межос. 100
К1-8	канализация — умывальник	516	450	Ø40
В1-8	холодная вода — умывальник	566	550	межос. 100
Св64	светильник настенный	666	1860	гр. 4

Условные обозначения

- вывод кабеля для подключения прибора (без розетки), марка ЭВ
- светильник настенный (бра), Н — высота оси
- вывод В1 (код — в ведомости привязок)
- вывод Т3 (код — в ведомости привязок)
- вывод К1 (код — в ведомости привязок)
- привязки точек и выводов от угла и от пола, мм
- А — марка развёртки: буква стены, стрелка — взгляд

Схема развёрток (М 1:50)

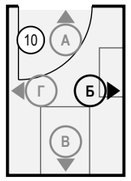

Примечания

1. Вид «Привязки» стены Б — электроточки и выводы ВК; архитектурная развёртка (мебель, отделка, проёмы, высоты) — на листе 83. Мебель и приборы — подложкой для ориентира; их марки и обозначения мебели, проёмов и стен — там же.
2. Привязки — в мм: по горизонтали от левого чистового угла стены до оси изделия, Н — от чистого пола до оси; все точки — в таблице привязок. Красная цепочка — привязки по осям; точки ближе 120 мм одна к другой в цепочку не дробятся — их привязки только в таблице.
3. У знака — марка электроточки (Р — розетка, S — выключатель, Св — светильник, ЭВ — вывод кабеля); условные обозначения и общие указания — лист 3.
4. Коды выводов ВК: В1 — холодная вода, Т3 — горячая вода, К1 — канализация; номер после дефиса — номер вывода на листе выводов сантехники.

					Проект: Четырёхкомнатная квартира — М 1:20
	Лист	№ док.	Подпись	Дата	Привязки электроточек и выводов ВК, стена Б. Санузел (пом. 10)
Дизайнер	Кырлан А.С.			04.11.26	Стадия: П; Лист: 84; Листов: 120

Развёртка стены Г

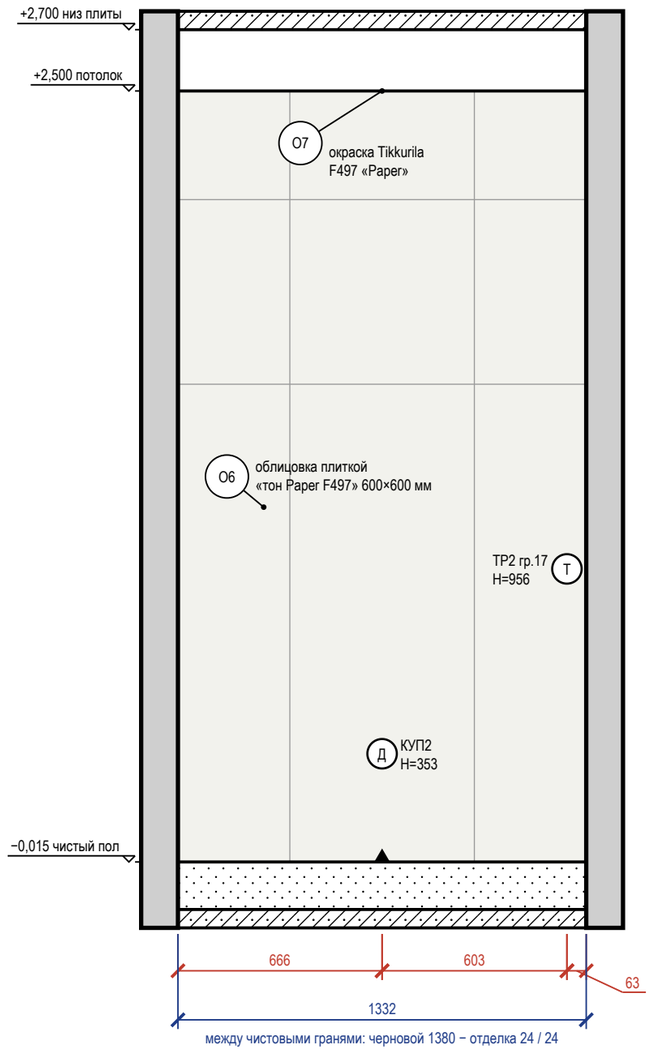


Схема развёрток (М 1:100)



Ведомость отделки (на листе)

Марка	Поверхность	Материал, изделие	Цвет, код	Кол.
О6	стены	облицовка плиткой, 600×600×9 мм, аналог: керамогранит матовый, тон F497, затирка CG2WA	#F1F1EC «тон Paper F497»	3,3 м²
О7	потолок	окраска, Tikkurila Luja 7, матовая, подготовка Q3	Tikkurila F497 «Paper»	1,3 м²

Примечания

1. Размеры — в мм от чистовых поверхностей стен; условные обозначения и общие указания — лист 3.
2. Облицовка — по сетке швов 2 мм, раскладка от оси стены (треугольник у пола), по высоте — от середины облицовки, подрезки у пола и у потолка поровну; подрезки — по листу раскладки плитки.
3. Гидроизоляция в 2 слоя, заход на стены 200 мм — до облицовки, с актом скрытых работ и тестом проливом (узел — на листе узлов).

					Проект: Четырёхкомнатная квартира	М 1:20
	Лист	№ док.	Подпись	Дата		
Дизайнер	Кырлан А.С.			04.11.26	Развёртка стены Г. Санузел (пом. 10)	Стадия: П; Лист: 85; Листов: 120

Развёртка стены А


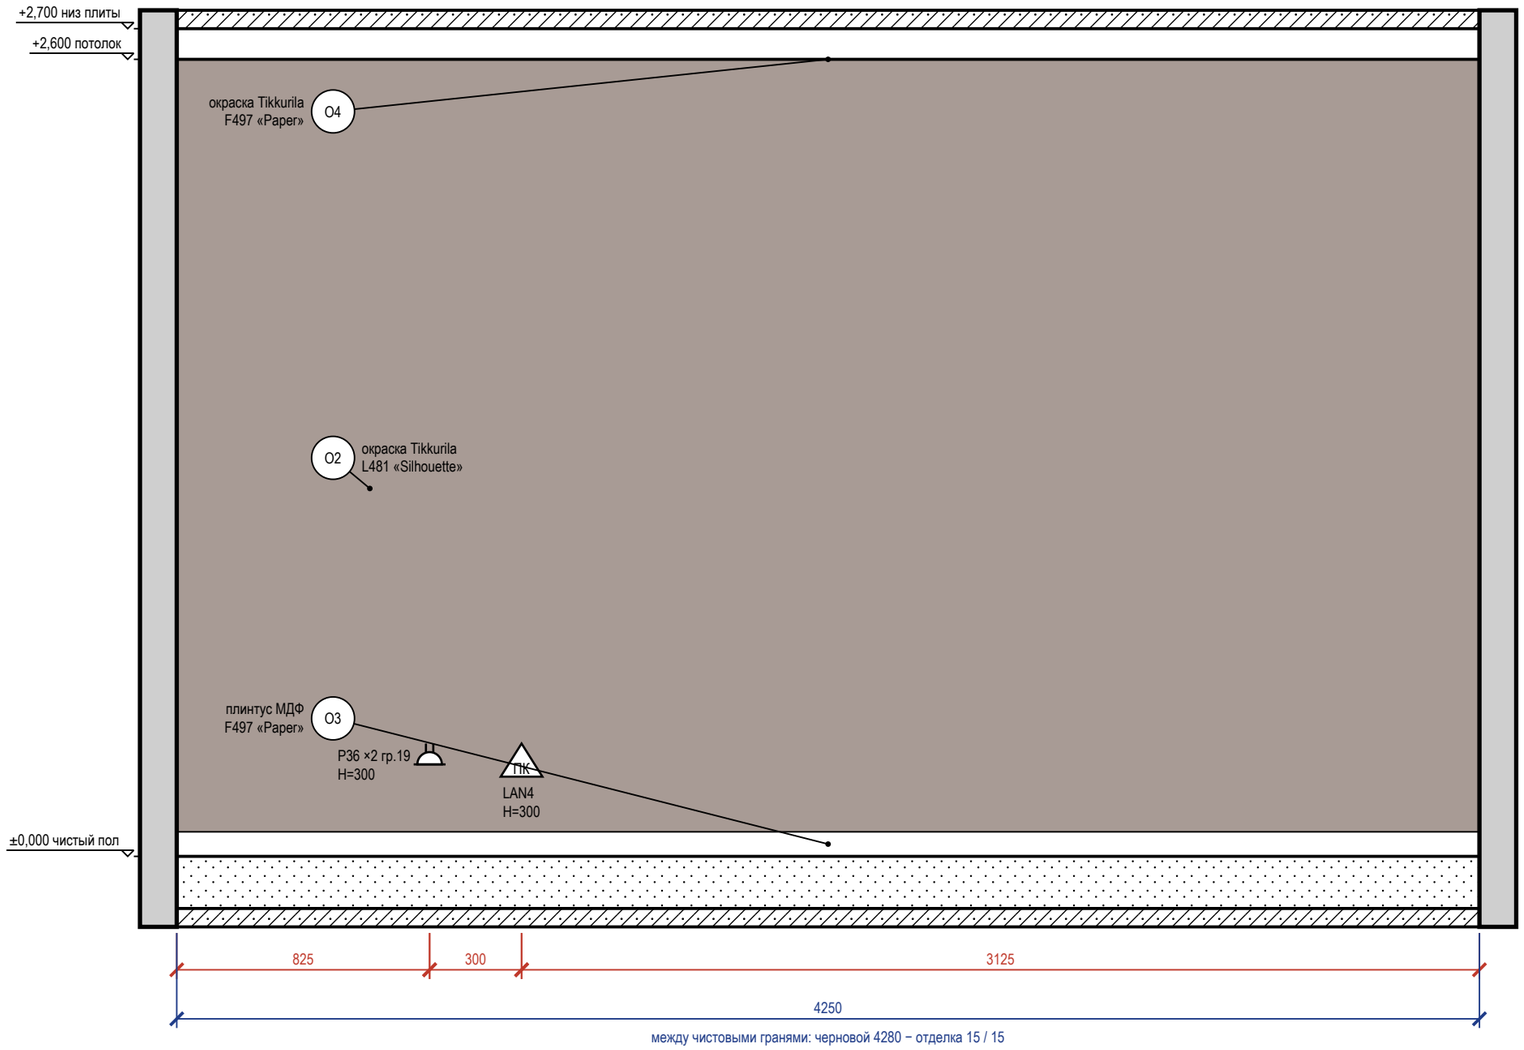


Схема развёрток (М 1:100)

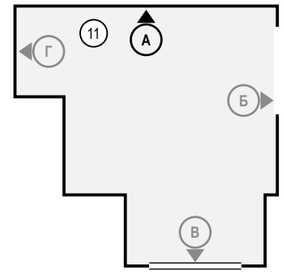

Ведомость отделки (на листе)

Марка	Поверхность	Материал, изделие	Цвет, код	Кол.
О2	акцентная стена	окраска, Tikkurila Optiva 5 Matt, аналог: интерьерная краска, класс 2 по EN 13300, глубокоматовая/матовая, база С, матовая, подготовка К3	Tikkurila L481 «Silhouette»	11,1 м²
О3	плинтус	плинтус МДФ, h 80 мм, аналог: плинтус МДФ под окраску 80×16 мм, полуглянцевая	Tikkurila F497 «Paper»	4,3 м
О4	потолок	окраска, Tikkurila Anti-Reflex 2, глубокоматовая, подготовка Q3	Tikkurila F497 «Paper»	14,6 м²

Примечания

1. Размеры — в мм от чистовых поверхностей стен; условные обозначения и общие указания — лист 3.

	Лист	№ док.	Подпись	Дата
Дизайнер	Кырлан А.С.			04.11.26

Проект: Четырёхкомнатная квартира — М 1:20

Развёртка стены А. Гостиная (пом. 11)

Стадия	Лист	Листов
П	86	120

Развёртка стены Б


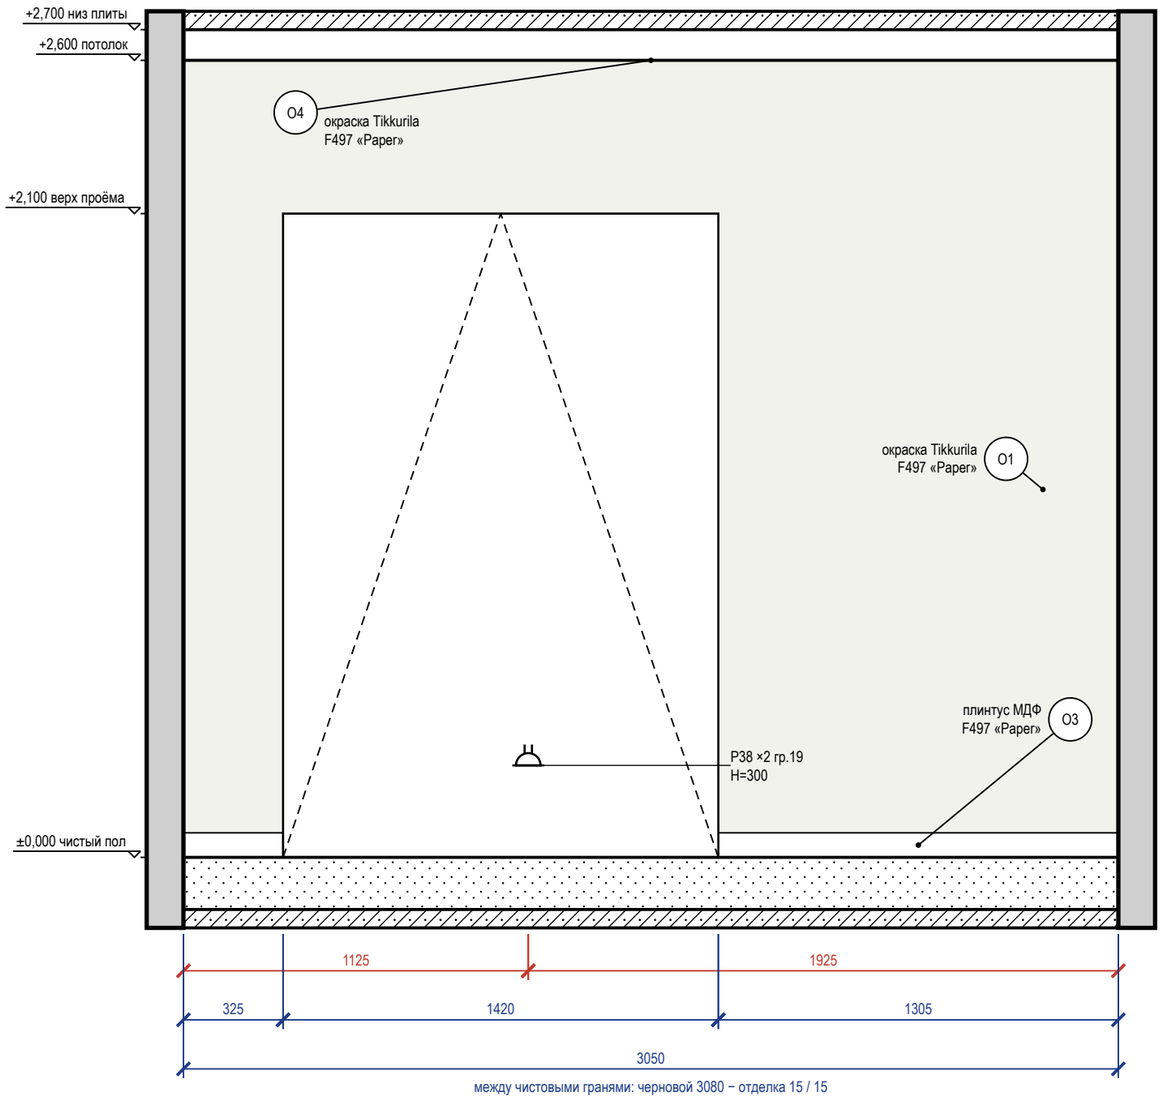


Схема развёрток (М 1:100)

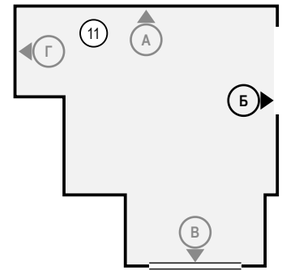

Ведомость отделки (на листе)


Марка	Поверхность	Материал, изделие	Цвет, код	Кол.
О1	стены	окраска, Tikkurila Optiva 5 Matt, матовая, подготовка К3	Tikkurila F497 «Paper»	4,9 м²
О3	плинтус	плинтус МДФ, h 80 мм, аналог: плинтус МДФ под окраску 80×16 мм, полуглянцевая	Tikkurila F497 «Paper»	1,6 м
О4	потолок	окраска, Tikkurila Anti-Reflex 2, глубокоматовая, подготовка Q3	Tikkurila F497 «Paper»	14,6 м²

Примечания

1. Размеры — в мм от чистовых поверхностей стен; условные обозначения и общие указания — лист 3.

					Проект: Четырёхкомнатная квартира — М 1:20
	Лист	№ док.	Подпись	Дата	
Дизайнер	Кырлан А.С.			04.11.26	Развёртка стены Б. Гостиная (пом. 11)
					Стадия: П; Лист: 87; Листов: 120

Развёртка стены В

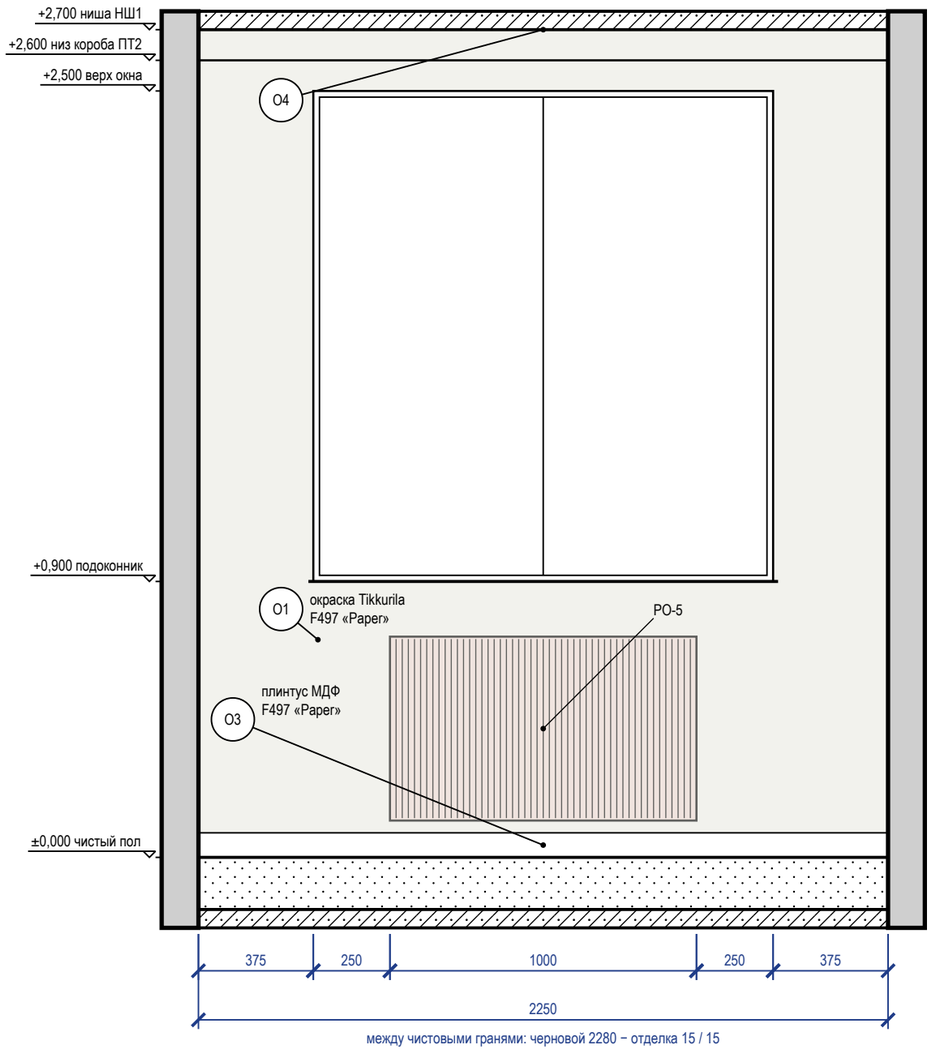

Развёртка стены Г


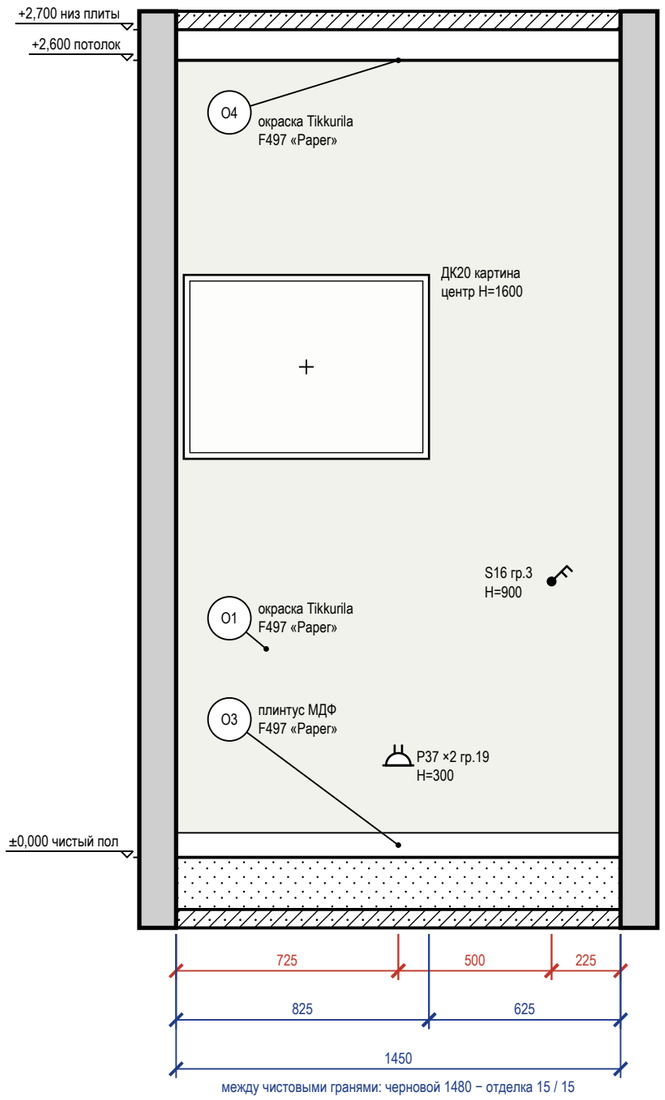


Схема развёрток (М 1:100)

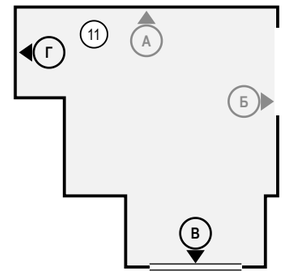

Ведомость отделки (на листе)

Марка	Поверхность	Материал, изделие	Цвет, код	Кол.
О1	стены	окраска, Tikkurila Optiva 5 Matt, матовая, подготовка К3	Tikkurila F497 «Paper»	7,4 м²
О3	плинтус	плинтус МДФ, h 80 мм, аналог: плинтус МДФ под окраску 80×16 мм, полуглянцевая	Tikkurila F497 «Paper»	3,7 м
О4	потолок	окраска, Tikkurila Anti-Reflex 2, глубокоматовая, подготовка Q3	Tikkurila F497 «Paper»	14,6 м²

Примечания

1. Размеры — в мм от чистовых поверхностей стен; условные обозначения и общие указания — лист 3.
2. Картины и зеркала крепить к основанию по паспорту изделия (закладные и анкеры — в перечне скрытых работ); крест — ось центра предмета.


	Лист	№ док.	Подпись	Дата
Дизайнер	Кырлан А.С.			04.11.26

Проект: Четырёхкомнатная квартира — **М 1:20**

Развёртки стен В, Г. Гостиная (пом. 11)


Стадия	Лист	Листов
П	88	120

Развёртка стены А

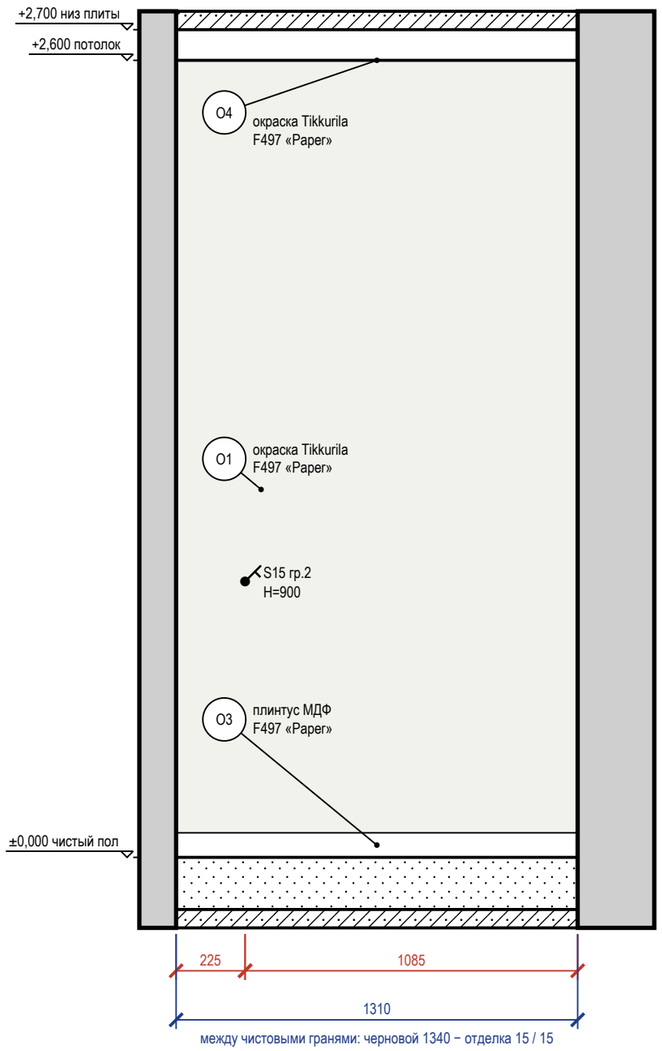


между чистовыми гранями: черновой 1340 − отделка 15 / 15

Развёртка стены Б

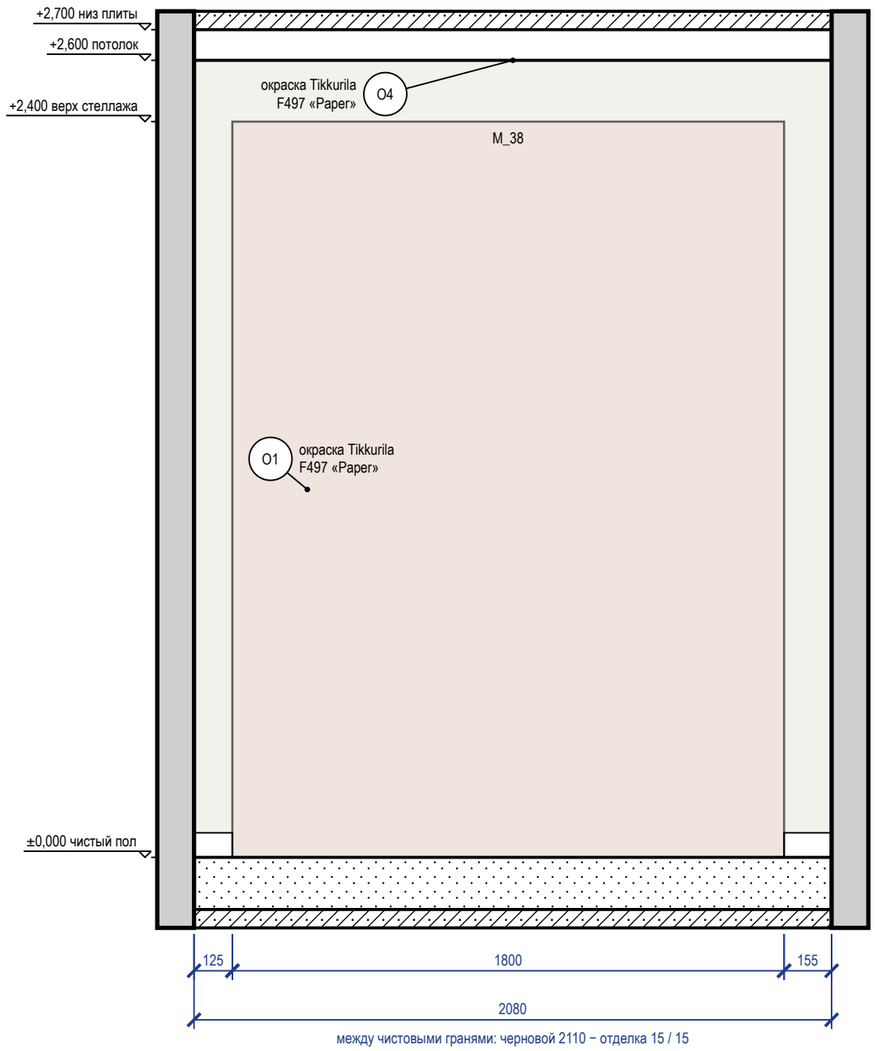


между чистовыми гранями: черновой 2110 − отделка 15 / 15

Развёртка стены В

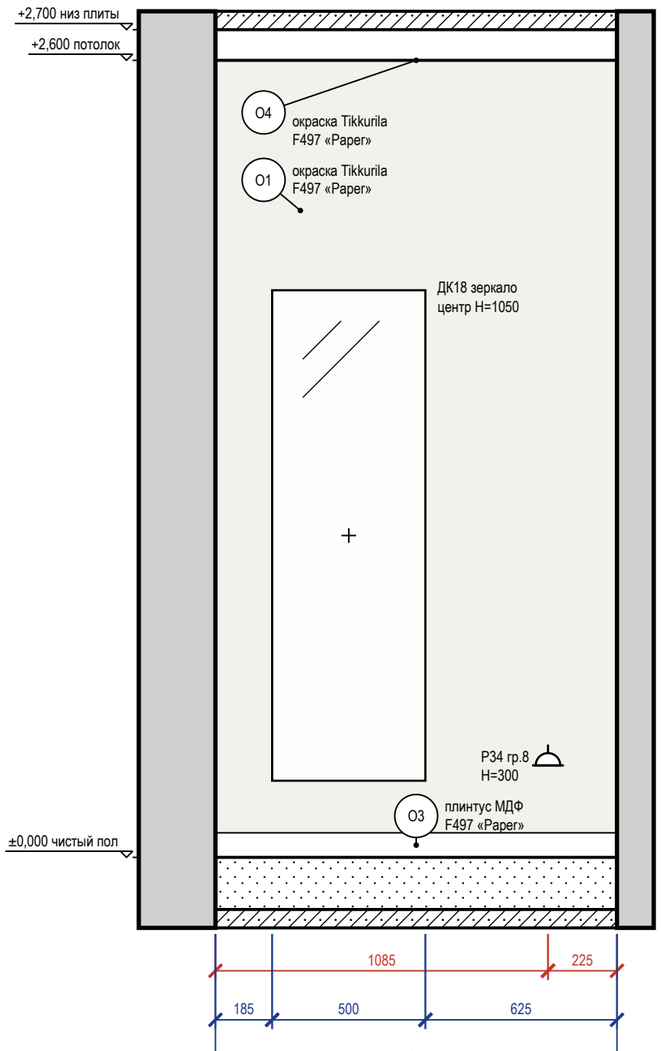

между чистовыми гранями: черновой 1340 − отделка 15 / 15

Схема развёрток (М 1:100)

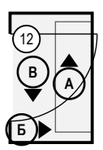

Ведомость отделки (на листе)

Марка	Поверхность	Материал, изделие	Цвет, код	Кол.
О1	стены	окраска, Tikkurila Optiva 5 Matt, матовая, подготовка К3	Tikkurila F497 «Paper»	12,2 м²
О3	плинтус	плинтус МДФ, h 80 мм, аналог: плинтус МДФ под окраску 80×16 мм, полуглянцевая	Tikkurila F497 «Paper»	2,9 м
О4	потолок	окраска, Tikkurila Anti-Reflex 2, глубокоматовая, подготовка Q3	Tikkurila F497 «Paper»	2,8 м²


Примечания

1. Размеры — в мм от чистовых поверхностей стен; условные обозначения и общие указания — лист 3.
2. Картины и зеркала крепить к основанию по паспорту изделия (закладные и анкеры — в перечне скрытых работ); крест — ось центра предмета.

					Проект: Четырёхкомнатная квартира	М 1:20
	Лист	№ док.	Подпись	Дата		
Дизайнер	Кырлан А.С.			04.11.26	Развёртки стен. Гардеробная 1 (пом. 12)	

Стадия	Лист	Листов
П	89	120

Развёртка стены А

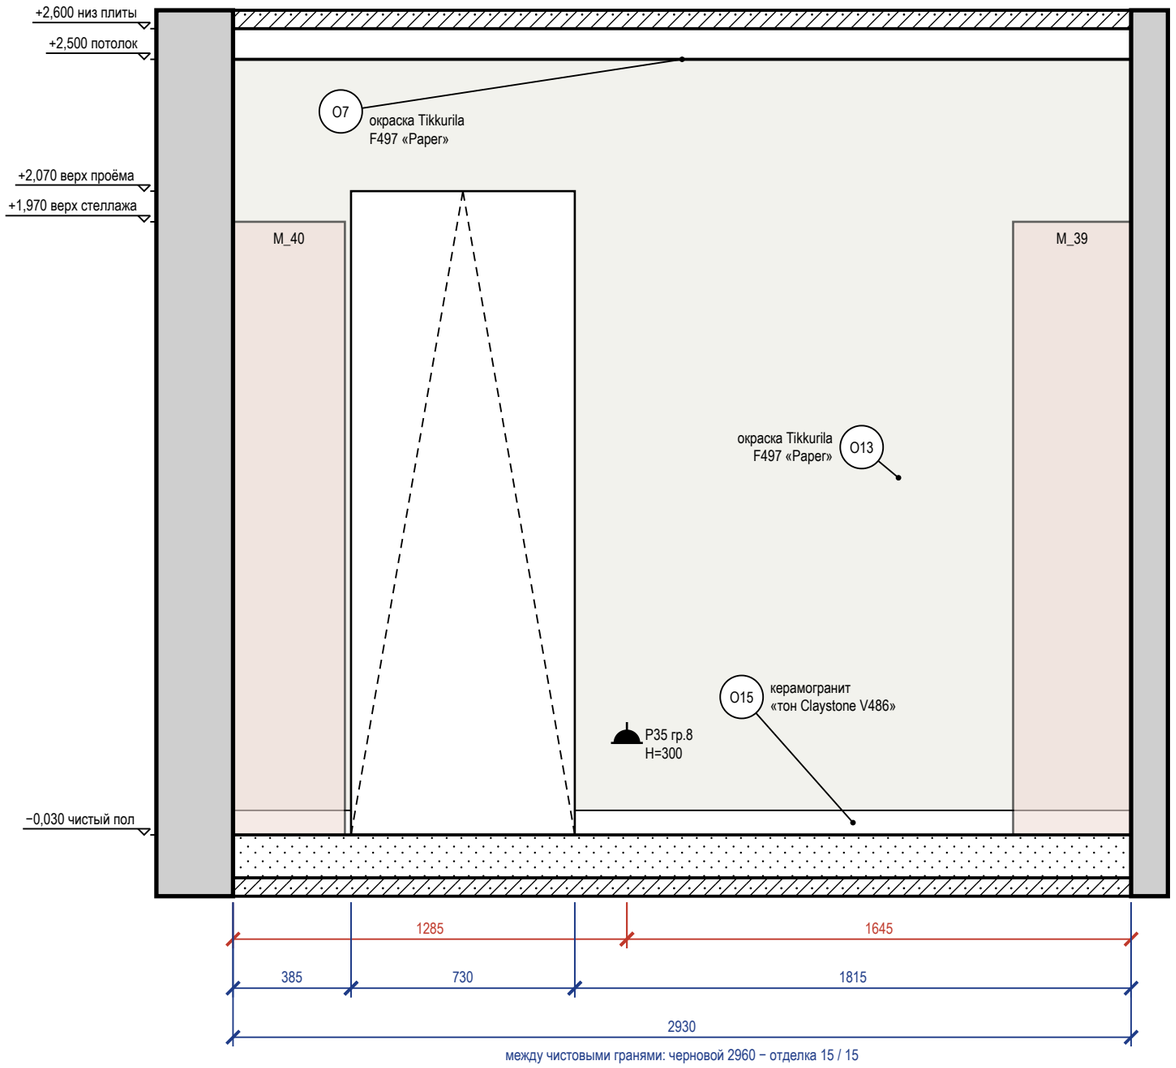

Развёртка стены Б


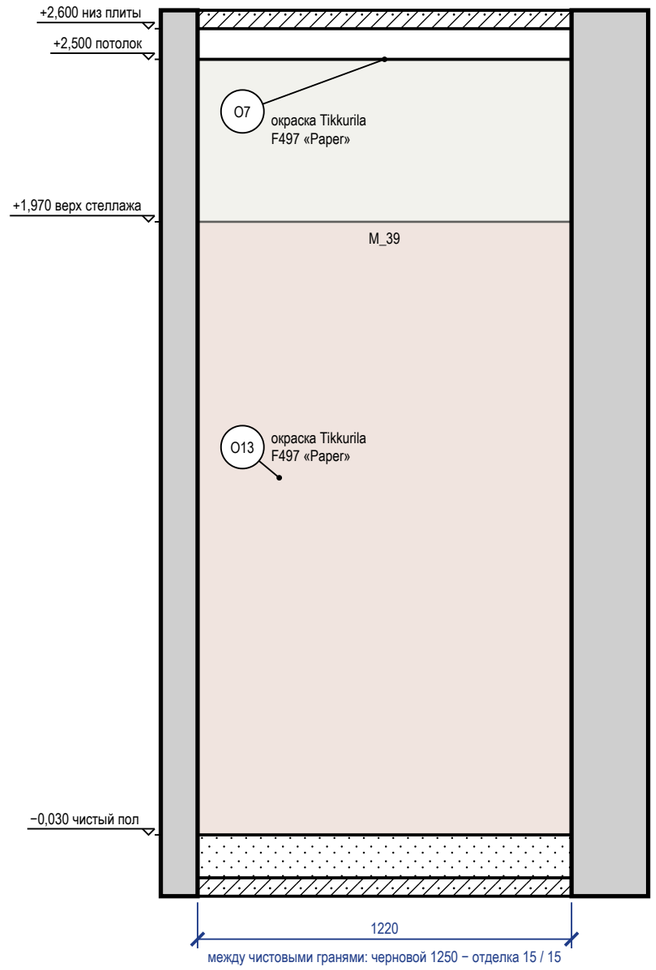


Схема развёрток (М 1:100)

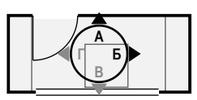

Ведомость отделки (на листе)

Марка	Поверхность	Материал, изделие	Цвет, код	Кол.
O7	потолок	окраска, Tikkurila Luja 7, матовая, подготовка Q3	Tikkurila F497 «Paper»	3,7 м²
O13	стены	окраска, Tikkurila Luja 7, шелковисто-матовая, подготовка K3	Tikkurila F497 «Paper»	9 м²
O15	плинтус	керамогранит, аналог: плинтус из керамогранита пола, подрезка 80 мм, верхняя кромка с запилом 45°	#B8AFA5 «тон Claystone V486»	2,2 м


Примечания

1. Размеры — в мм от чистовых поверхностей стен; условные обозначения и общие указания — лист 3.

					Проект: Четырёхкомнатная квартира	М 1:20
	Лист	№ док.	Подпись	Дата		
Дизайнер	Кырлан А.С.			04.11.26	Развёртки стен А, Б. Балкон 1 (пом. 13)	
					Стадия: П; Лист: 90; Листов: 120	

выпуск 04.11.2026 № 2391fcbada · стр. 90 из 120

Развёртка стены В

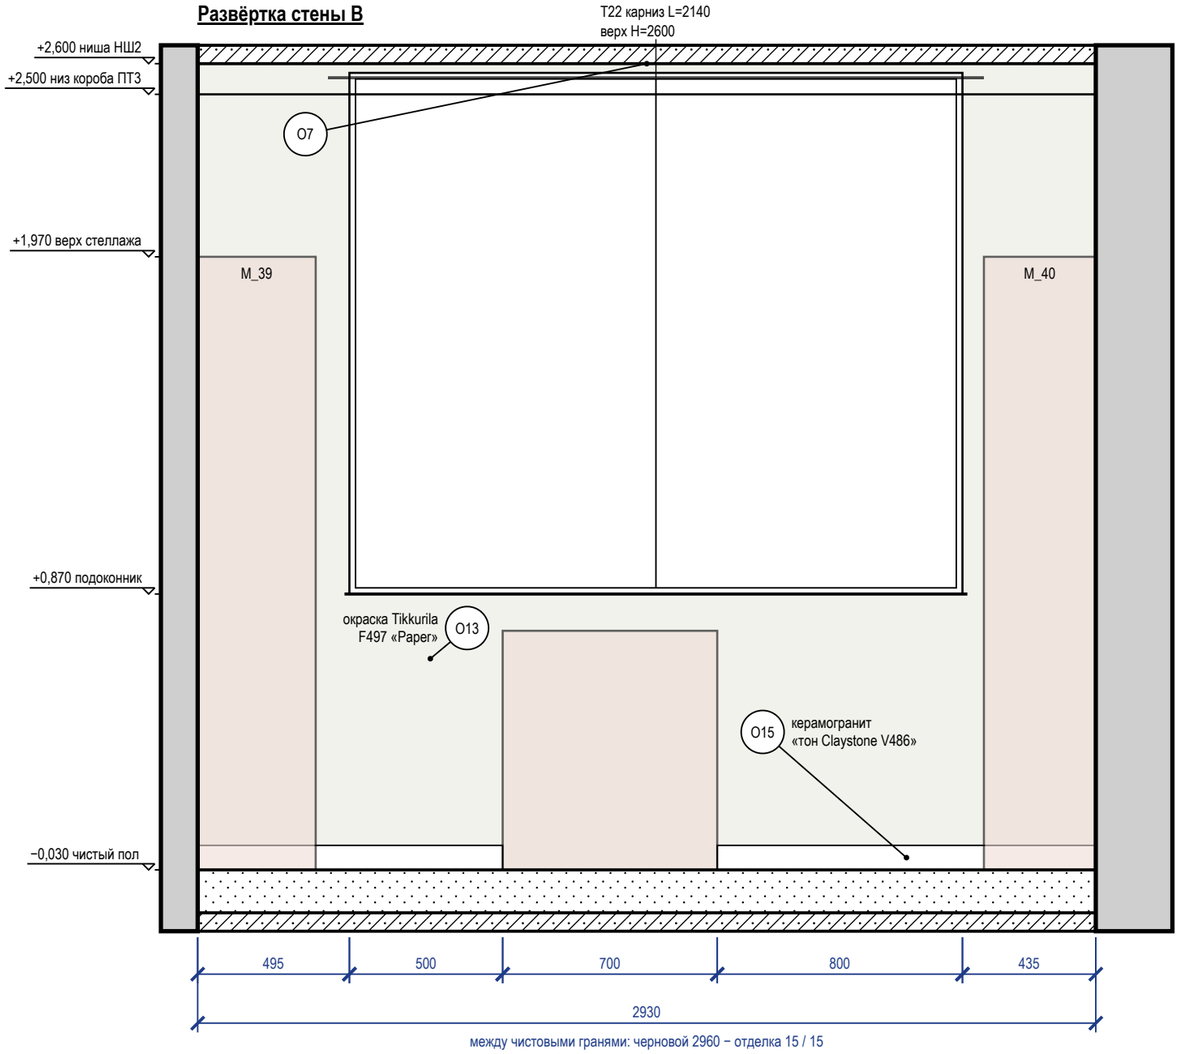

Развёртка стены Г


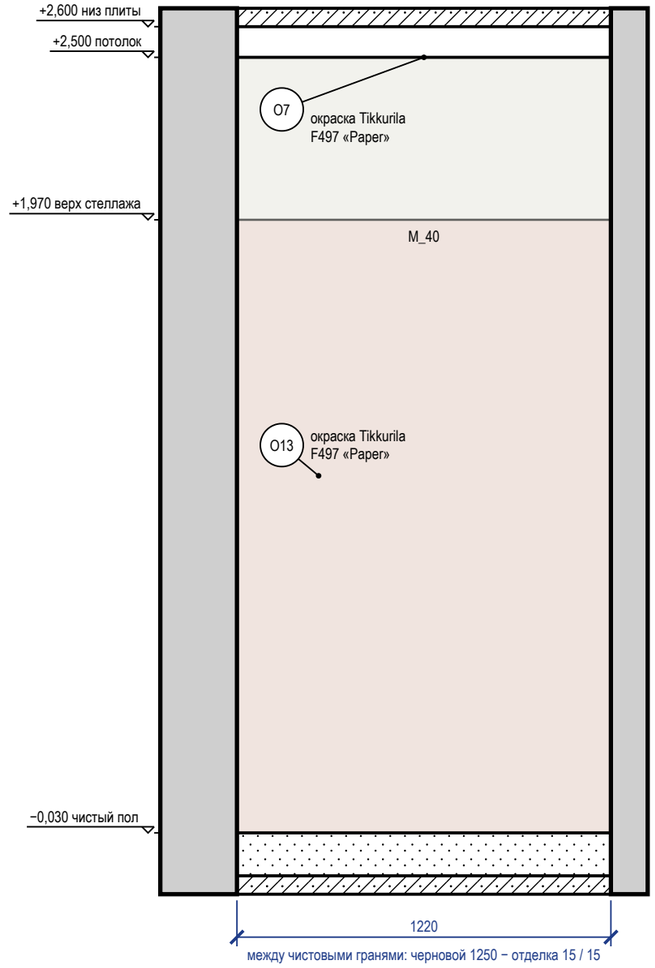


Схема развёрток (М 1:100)

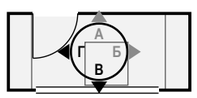

Ведомость отделки (на листе)

Марка	Поверхность	Материал, изделие	Цвет, код	Кол.
О7	потолок	окраска, Tikkurila Luja 7, матовая, подготовка Q3	Tikkurila F497 «Paper»	3,7 м²
О13	стены	окраска, Tikkurila Luja 7, шелковисто-матовая, подготовка К3	Tikkurila F497 «Paper»	7,4 м²
О15	плинтус	керамогранит, аналог: плинтус из керамогранита пола, подрезка 80 мм, верхняя кромка с запилом 45°	#B8AFA5 «тон Claystone V486»	2,2 м

Примечания

1. Размеры — в мм от чистовых поверхностей стен; условные обозначения и общие указания — лист 3.
2. Карнизы (шины) — по ведомости текстиля декоратора: длина L и верх H на развёртке — те же числа, что в ведомости; крепление — до окраски потолка.

					Проект: Четырёхкомнатная квартира	М 1:20
	Лист	№ док.	Подпись	Дата		
Дизайнер	Кырлан А.С.			04.11.26	Развёртки стен В, Г. Балкон 1 (пом. 13)	Стадия: П; Лист: 91; Листов: 120

Комплект предварительный по пунктам этих таблиц. Пока по пункту нет ответа или решения, показанное на указанном листе — допущение проектировщика, а не утверждённое решение.
Сводка: открытых вопросов — 27 (из них ждут факта объекта — 15: контрольного обмера, обследования или документа); конфликтов между разделами — 1; изменений в реестре — 20, из них без подписи — 7; разделов, не сданных к выпуску, — 1.

Открытые вопросы и принятые допущения

№	Формулировка	Вид	Кто решает	Если решения нет	Лист, где это проявляется
К-1	Окно детской 2 (поз. 9) на наружной стене В: привязки 1580…3080 в источниках нет — в экспликации скана окна этой комнаты не показано. Это допущение проектировщика, центровка, а не замер: окно 1500 мм поставлено примерно по центру наружного участка стены В (по контуру 8030–10610 по оси Х, центр 9320; окно 8540–10040, центр 9290). Размер 1500×1600 и подоконник 800 мм взяты из исходной записи окна, источник размера в данных не указан. Из допущения следует конфликт со стояками Ст К1-2 и Ст В1-2 (9400; 6300) и (9560; 6300): они попадают в проём окна вместе с коробом и люком (конфликт Кф-1, вопрос К-15). Нужен контрольный обмер эркера: положение, размер и подоконник окна, затем осей стояков.	Непонятно Ждёт: обмера	Архитектор-планировщик	Остаётся принятое положение окна как допущение, не замер. Конфликт со стояками Кф-1 не снят: радиатор под окном, шторы и короб со стояками на этом месте не совмещаются.	л. 6 — План планировки от заказчика
К-3	Несущие стены не определены (нет плана БТИ и техзаключения): до их получения демонтаж не планируется. Нужно: запросить проект дома и поэтажный план БТИ, установить серию дома; несущие стены и допустимость вмешательства определяет техническое заключение специализированной организации. Тип дома (монолит) и перекрытие (монолитная плита 220 мм) в данных приняты допущением: источника — проекта дома, плана БТИ, обследования — в материалах объекта нет; материал основания стен и перекрытия определит тот же документ или обследование.	Отсутствует Ждёт: документа, обследования	Архитектор-планировщик	Исходных данных нет: на листе нет решения по этому пункту или оно условное; лист предварительный.	полный альбом
К-4	Гостиная (поз. 11): мебели в модели нет, расстановка ждёт решения заказчика. Отделка, потолок, свет, розетки и декор выполнены; акцентная стена А L481 возвращена (см. К-7); картина ДК20, ваза ДК21 и подсветка картины — предложение конвейера (ИЗ-7). Площадь по модели 14,55 м² (≈17 м² по реконструкции контура — снимет контрольный обмер).	Отсутствует Ждёт: решения	Дизайнер интерьера	Исходных данных нет: на листе нет решения по этому пункту или оно условное; лист предварительный.	л. 16 — План размещения мебели и оборудования
К-5	Гардеробная 1 (поз. 12) в натуре трапеция 2320/2132/1400, в модели прямоугольник той же площади: нужен контрольный обмер углов.	Непонятно Ждёт: обмера	Архитектор-планировщик	Остаётся значение, принятое по исходным данным; оно не подтверждено, лист предварительный.	л. 6 — План планировки от заказчика
К-6	Розетка Р7 (стиральная машина, ванная комната) стоит в 72 мм от угла при норме от 150 мм. Р7 возвращена на прежнее место: стена В, смещение 2543 мм, высота 949 мм — норма ПУЭ 6.6.30 (не выше 1 м) выполнена, флага решения нет; конвейер уходил от угла переносом на 2242 мм и высоту 1250 мм, что нарушало ПУЭ 6.6.30, — этот перенос отменён. Нужно решение автора: сдвинуть машину и розетку от угла или принять 72 мм. Норма для розеток ванной (ПУЭ 7.1.48 против BS 7671) решена: ИЗ-19.	Спорно Ждёт: решения	Инженер-электрик	Р7 остаётся на 2543 мм вдоль стены и 949 мм по высоте, в 72 мм от угла: замечание открыто.	л. 43 — План розеток и электровыводов
К-7	Акцент L481 занимает больше порога 15 % площади поверхностей на акцентной стене А Гостиной — 16 % (проверка по доле акцента, замечание открыто намеренно). Красить плоскость целиком (нужна поддержка в модели), перенести акцент на предметы (в Гостиной они уже есть — ДК20, ДК21, ИЗ-7) или принять 16 %. Для Зала решение принято: 18 % приняты автором (ИЗ-15).	Спорно Ждёт: решения	Колорист-комплектатор	Остаётся акцентная стена L481 в Гостиной, доля 16 % выше порога 15 %; замечание открыто.	л. 14, 15 — Колерная карта
К-8	Графы «Пров.» и «Н. контр.» в штампе пусты: их заполняет человек, подписи проверяющего и нормоконтролёра автор проекта не ставит; для выдачи нужны разные подписанты, отличные от разработчика. Решение автора (ИЗ-18): графы остаются пустыми, комплект предварительный.	Отсутствует Ждёт: решения	Нормоконтролёр	графы остаются пустыми; комплект предварительный, не проверен независимо	л. 3 — Список листов
К-10	Прямые углы помещений с кухней, санузлами, гардеробными и встроенной мебелью по скану не подтверждены (скос стен приведён к ступеням): ванная комната, тёмная комната, детская 1, коридор, кухня, прихожая-коридор, гардеробная 2, детская 2, гардеробная 1, балкон 1. Нужен контрольный обмер: длины сторон, обе диагонали, отклонения углов от 90° у стен под встроенную мебель и плитку; только после него отмечаются углы 90°.	Отсутствует Ждёт: обмера	Архитектор-планировщик	Исходных данных нет: на листе нет решения по этому пункту или оно условное; лист предварительный.	л. 6 — План планировки от заказчика
К-12	Состав подрядчиков и поставщиков (кто покупает и кто монтирует радиаторы, подоконники, двери, розетки) от заказчика не получен. Принята типовая схема частного ремонта (ИЗ-17): материалы и оборудование покупает заказчик по спецификациям проекта, монтаж ведёт подрядная бригада, приёмку скрытых работ ведёт автор. Схема уточняется договором подряда: нужен договор или состав подрядчиков и поставщиков от заказчика.	Отсутствует Ждёт: решения	Прораб-координатор	остаётся типовая схема: покупает заказчик, монтирует подрядная бригада, скрытые работы принимает автор; закрепление за конкретными подрядчиками не подтверждено	л. 3 — Список листов
К-13	Детская 2: рабочий стол M_35 у стены Б получает боковой свет от окна справа от сидящего; для правши лучше свет слева подтвердить, кто сидит за столом (правша или левша), иначе решить зеркальной расстановкой (нужен перенос двери) либо второй лампой слева.	Спорно Ждёт: решения	Дизайнер интерьера	Остаётся вариант, показанный на листе; он не утверждён, лист предварительный.	л. 16 — План размещения мебели и оборудования
К-14	Из чего стены под навесными шкафами — Ванная комната (стена Б, M_07), Кухня (стена А, M_23, M_24, M_25), Гардеробная 2 (стена В, M_32)? Проекта дома нет, на скане материал и толщина не читаются. Нужно обследование: материал основания определяет крепёж (анкер по бетону, закладная в ГКЛ). До ответа материал в данных не указан, замечание открыто намеренно.	Отсутствует Ждёт: вскрытия	Мебельщик	Исходных данных нет: на листе нет решения по этому пункту или оно условное; лист предварительный.	л. 8 — Кухня (пом. 6). Монтажная схема л. 9 — Кухня (пом. 6). Монтажная схема л. 10–12 — Шкафы. Монтажная схема
К-15	Стояки Ст К1-2 и Ст В1-2 (в данных (9400; 6300) и (9560; 6300), короб и люк) попадают в проём окна Детской 2 по стене В (8540–10040): совместить с радиатором под окном и шторами нельзя. Привязку осей стояков от двух стен никто не замерял; в Санузле они не стоят, выпуск унитаза С_06 от этого положения — 2,4 м. Нужен контрольный обмер стояков и окна, затем решение: сдвинуть окно, перенести радиатор или обойти короб.	Спорно Ждёт: обмера, затем решения	Инженер ВК (вода, канализация)	Остаются принятые положения окна и стояков без замера; радиатор под окном, шторы и короб со стояками на этом месте не совмещаются.	л. 22 — План выводов сантехники л. 23 — Схема разводки водопровода и канализации л. 6 — План планировки от заказчика
К-17	Ведущий цвет — Paper F497 на стенах и потолке — занимает больше 80 % площади поверхностей в Тёмной комнате (87 %), Гардеробной 2 (89 %), Гардеробной 1 (86 %) и Балконе 1 (85 %): второй цвет почти не читается. Это цвета автора проекта. Принять как есть или задать этим помещениям второй цвет.	Спорно Ждёт: решения	Колорист-комплектатор	Остаются цвета автора: стены и потолок в Paper F497, доля ведущего цвета 85–89 %.	л. 14, 15 — Колерная карта

					Проект: Четырёхкомнатная квартира
	Лист	№ док.	Подпись	Дата	Открытые вопросы, принятые допущения и конфликты. Лист 1 из 5
Дизайнер	Кырлан А.С.			04.11.26	

Стадия	Лист	Листов
П	92	120

Открытые вопросы и принятые допущения (продолжение)

№	Формулировка	Вид	Кто решает	Если решения нет	Лист, где это проявляется
К-18	Вытяжка M_24 встроена в навесной модуль на отметке 1550 мм: её низ над электрической варочной панелью 610 мм, а фартук 650 мм при практике 450–600 мм. Модель вытяжки не выбрана, паспорта нет, допустимая высота над варочной неизвестна. Поднять модуль M_24 (и соседние M_23, M_25 — на единую отметку), либо выбрать вытяжку, допускающую 610 мм по паспорту.	Спорно Ждёт: данных закупки, затем решения	Мебельщик	Остаётся модуль на отметке 1550 мм; низ вытяжки 610 мм над панелью, меньше 650 мм; допустимость высоты не подтверждена.	л. Д_14, Д_15 — Д_14 Кухня (пом. 6). Развёртка гарнитура
К-19	Привязка угла помещения «Гостиная» (поз. 12 скана; в примечании проекта названо «зал») принята в точке (10670; 3470) мм — это допущение, не замер: по пиксельной привязке скана угол может лежать примерно на 700 мм левее. От этой точки по оси X отсчитываются Гостиная и Гардеробная 1, по ней же проходит стена Детской 2 со стороны Гостиной. Нужен контрольный обмер: расстояние от опорной стены до этого угла.	Непонятно Ждёт: обмера	Архитектор-планировщик	Остаётся угол в точке (10670; 3470) как допущение: размеры правой части на листах — расчётные, возможен сдвиг до ≈700 мм; мебель, свет и розетки там привязаны к принятым координатам.	л. 6 — План планировки от заказчика
К-20	Наружные скошенные стены (в натуре под 45°) заменены на планах ступенями: движок описывает только ортогональную геометрию. Гостиная — три ступени, площадь по модели 14,55 м² против ≈17 м² по реконструкции контура; Гардеробная 1 — прямоугольник 1400×2230 вместо трапеции 2320/2132/1400 той же площади (К-5). Углы и длины скосов на листах не показаны, площади у скошенных стен условные (К-10). Принять ступени как условность до обмера или передать скосы обмером и отдельным чертежом.	Спорно Ждёт: решения	Архитектор-планировщик	Остаются ступени вместо скоса: фактическая форма наружных стен Гостиной и Гардеробной 1 на листах не показана, размеры вдоль скоса брать по обмеру на месте.	л. 6 — План планировки от заказчика л. 16 — План размещения мебели и оборудования
К-21	Все размеры сняты с размерных цепочек растрового скана заказчика, контрольного обмера нет. Площади помещений и «Общая площадь 102,67 м²» в штампе каждого листа — расчётные по модели, не обмерные: итог зависит от ступеней вместо скоса (К-20) и принятого угла Гостиной (К-19). Названия и номера помещений со сканом не сверены (общая комната назначена решением автора, ИЗ-13). Толщины стен приняты допущением: наружные 250 мм, внутренние 120 мм, источника (обмер, проект дома) нет. Всё, что на листах выглядит как замер, снято со скана.	Отсутствует Ждёт: обмера	Архитектор-планировщик	Размеры и площади остаются ориентировочными; штамп печатает «Общая площадь 102,67 м²» как расчётную величину, не подтверждённую обмером; до обмера не заказывать материалы и изделия по размерам листов.	л. 3 — Список листов л. 6 — План планировки от заказчика
К-22	Окно Гостиной (пом. 11) на стене В, часть 2: остекление показано по обмерному скану, размеры 1500×1600 мм и подоконник 900 мм приняты типовыми, не замерены. Нужен контрольный обмер окна: положение, ширина, высота, подоконник.	Непонятно Ждёт: обмера	Архитектор-планировщик	Остаются типовые размеры окна 1500×1600 мм, подоконник 900 мм; на плане они напечатаны как принятые, не замеренные.	л. 6 — План планировки от заказчика
К-23	Две розетки выше 1 м от пола остаются предложением проектировщика, решения автора нет: Р21 (вытяжка M_24, 2200 мм, в модуле за съёмной панелью, Кухня) и Р27 (слаботочный щит ЩС, 1600 мм, Прихожая-коридор). Основание — назначение розетки; автор высоту не подтверждал; основание записано в самой позиции (знак «**» у марки, примечание листа). Норма (ПУЭ, п. 6.6.30) — не выше 1 м. Подтвердить высоты или опустить розетки.	Спорно Ждёт: решения	Инженер-электрик	Высоты остаются как на листе, решение автором не подтверждено.	л. 43 — План розеток и электровыводов полный альбом
К-24	Высота потолка 2700 мм принята: источника (замер, проект дома) в материалах объекта нет. От неё зависят вертикальные размеры альбома: развёртки, шкафы и встроенная мебель, плитка, потолки, объёмы работ. Замерить высоту на объекте в каждом помещении.	Непонятно Ждёт: обмера	Архитектор-планировщик	Высота 2700 мм остаётся принятой, не замеренной: вертикальные размеры листов и объёмы работ ориентировочные; встроенную мебель и плитку по высоте не заказывать до замера.	л. 6 — План планировки от заказчика
К-25	Разрешённая мощность 15 кВт принята, технических условий в материалах объекта нет; расчётная мощность 11,2 кВт. Сверить с техническими условиями.	Непонятно Ждёт: документа	Инженер-электрик	Разрешённая мощность 15 кВт остаётся принятой, не подтверждённой техническими условиями: вводной аппарат и группы щита предварительные.	л. 41, 42 — Однолинейная схема щита
К-26	Артикулы изделий отделки не выбраны. Инженерная доска (пом. 1, 3, 4, 6, 8, 9, 11, 12), керамогранит пола (пом. 2, 5, 7, 10, 13), керамогранит стен санузла и ванной (пом. 2, 10) и фартука кухни (пом. 6), плинтус МДФ (пом. 1, 3–9, 11, 12), плинтус из керамогранита (пом. 13) и краска акцентных стен (пом. 1, 11) заданы характеристиками — «аналог по характеристикам», кода изделия производителя нет. Цвет керамогранита назван тоном по колерной карте (J484, F497, V486), но тон — не артикул изделия. Артикул выбирается при закупке: выбрать изделия, вписать артикулы в ведомость отделки и спецификации, цвет и тон принять по образцу из партии. Количество к заказу и упаковки — расчётные, по номинальным размерам, до выбора изделия.	Отсутствует Ждёт: данных закупки, затем решения	Отделочник	материалы остаются описанными характеристиками; заказ по спецификации и подсчёт упаковок — только после выбора изделий	л. 51 — Раскладка плитки. Планы полов л. 52 — Раскладка плитки. Фартук кухни л. 32 — Раскладка плитки. Ванная комната. Развёртки стен л. 33 — Раскладка плитки. Санузел. Развёртки стен л. 50 — План покрытий пола л. С1, С2, С3 — С1–С3 Ведомость отделки помещений л. 14, 15 — Колерная карта л. С4, С5 — С4–С5 Спецификация отделочных материалов полный альбом
К-27	Модели встраиваемой техники кухни не выбраны: холодильник (M_19), духовой шкаф (M_21) и посудомоечная машина (M_26) заданы описанием «аналог по характеристикам» — без производителя, серии и кода. Размеры ниш и вентзазоры взяты по типовой схеме на 600 мм, а не по паспорту модели: у разных изготовителей они расходятся, и модуль, сделанный по типовой нише, может не принять выбранную технику. Вытяжка M_24 — отдельный вопрос К-18. Нужно: выбрать модели, получить монтажные схемы изготовителей и сверить ниши модулей, вентиляцию и подключение до заказа гарнитура.	Отсутствует Ждёт: данных закупки, затем решения	Мебельщик	ниши остаются по типовой схеме на 600 мм, не подтверждённой паспортом модели; модули кухни не заказывать до выбора техники	л. Д_14, Д_15 — Д_14 Кухня (пом. 6). Развёртка гарнитура л. 8 — Кухня (пом. 6). Монтажная схема
К-28	Санузел (пом. 10): унитаз С_06 при положении стояков по данным (К-15) имеет выпуск 3600 мм до стояка К1 и 2357 мм до стояка Ø110 по прямой; вход в санузел — только из Детской 2. Длинный выпуск требует нормативного уклона по всей длине (СП 30.13330) — подъёма пола санузла (подиум) или насосной установки. Решить: принять длинный выпуск с подиумом/насосом, перенести унитаз ближе к стояку или перепланировать санузел — после контрольного обмера стояков (К-15).	Спорно Ждёт: решения	Инженер ВК (вода, канализация)	выпуск С_06 остаётся 3600 мм: раскладка санузла и высота пола не утверждены, разводку канализации не выполнять до решения	л. 22 — План выводов сантехники л. 16 — План размещения мебели и оборудования л. 6 — План планировки от заказчика

					Проект: Четырёхкомнатная квартира
	Лист	№ док.	Подпись	Дата	Открытые вопросы, принятые допущения и конфликты. Лист 2 из 5
Дизайнер	Кырлан А.С.			04.11.26	

Стадия	Лист	Листов
П	93	120

Открытые вопросы и принятые допущения (продолжение)

№	Формулировка	Вид	Кто решает	Если решения нет	Лист, где это проявляется
К-29	Мойка кухонная C_05 (пом. 6 «Кухня»), выпуск К1-5 Ø50: в полу не помещается: врезка + перепад 202 (10,10 м × 20 мм/м) + Ø50 + слой над трубой 45 = 307 мм при пироге 170 мм. Решить: (а) подиум или подъём пола на 140 мм (ступень на входе — порог); (б) прибор ближе к стояку Ст К1-2; (в) насосная установка (КНС) у прибора — по паспорту, требует согласования. Решение меняет кухню (модули, цоколь, точки ЭОМ) — за автором с заказчиком.	Спорно Ждёт: решения	Инженер ВК (вода, канализация)	выпуск К1-5 и кухню в части мойки не выполнять до решения; остальное — по листам	л. 23 — Схема разводки водопровода и канализации л. 22 — План выводов сантехники
К-30	Посудомоечная машина ОБ_03 (пом. 6 «Кухня»), выпуск К1-6 Ø50: в полу не помещается: врезка + перепад 152 (7,60 м × 20 мм/м) + Ø50 + слой над трубой 45 = 257 мм при пироге 170 мм. Решить: (а) подиум или подъём пола на 90 мм (ступень на входе — порог); (б) прибор ближе к стояку Ст К1-2; (в) насосная установка (КНС) у прибора — по паспорту, требует согласования. Решение меняет кухню (модули, цоколь, точки ЭОМ) — за автором с заказчиком.	Спорно Ждёт: решения	Инженер ВК (вода, канализация)	выпуск К1-6 и кухню в части мойки не выполнять до решения; остальное — по листам	л. 23 — Схема разводки водопровода и канализации л. 22 — План выводов сантехники
К-31	Гостиная (пом. 11, 14,55 м²) в данных без двери и проёма: со всех сторон глухие стены (к детской 1 — стена А, к детской 2 — стена Г, к гардеробной 1 — стена Б), единственная дверь Д-4 ведёт из неё в гардеробную 1, у которой другого выхода нет — два помещения недостижимы из квартиры, при этом в них заведены розетки, свет, LAN и Wi-Fi. По скану внутренней стала стена Б детской 2 на участке 3530…5010 — возможно, там проём; но на этой стене утверждённая расстановка детской 2 (стеллаж M_37, стол M_35, выключатель S18 — ИЗ-1, ИЗ-2). Нужно: выяснить у заказчика вход в гостиную (из детской 2, из детской 1 или новый проём из коридора через перепланировку) и подтвердить обмером; до ответа дверь в данные не вносится.	Отсутствует Ждёт: обследования, затем решения	Архитектор-планировщик	гостиная и гардеробная 1 недостижимы: отделку, потолок, ЭОМ и мебель в них не выполнять; если вход — через детскую 2, расстановку детской 2 (ИЗ-1, ИЗ-2) пересматривать	л. 6 — План планировки от заказчика л. 7 — План монтажный л. 16 — План размещения мебели и оборудования

Конфликты между разделами

№	Формулировка	Разделы	Статус	Кто решает	Если решения нет	Лист, где это проявляется
Кф-1	Стояки Ст К1-2, Ст В1-2 с коробом и люком попадают в проём окна Детской 2 (стена В, 8540–10040): положение стояков и окна не замерено; вопрос К-15.	ВК; архитектура (окно Детской 2)	Открыт, круг 1	Инженер ВК (вода, канализация)	Положение окна — допущение, стояков — по скану без привязки; пока их не замерили, окно, радиатор под ним и короб со стояками на листах не согласованы.	л. 22 — План выводов сантехники л. 23 — Схема разводки водопровода и канализации

Изменения проекта после выпуска листов (реестр изменений)

№	Дата	Лист	Было	Стало	Кто решил, подпись
ИЗ-1	05.10.2026	л. 16 — План размещения мебели и оборудования	Окно Детской 2 на стене Б (смещение 900). Стол M_35 1400×650, стена Б, смещение 1000; кресло M_36 (9300; 4950); стеллаж M_37 1200×2100, стена В, смещение 960.	Окно на наружной стене В (1580…3080; положение — допущение, центровка, не замер). Стол M_35 1400×650 (размер и допуск глубины «Г 600–700» прежние), стена Б, смещение 1500; кресло M_36 (9150; 5450); стеллаж M_37 1200×2100 (размер прежний), стена Б, смещение 120. Основания. Стеллаж: на стене В теперь окно, прежнее место перекрывает проём; на стене Б он стоит в углу А/Б. Стол: перенесён вслед за окном на стену Б без изменения размера; при 650 мм край стола заходит на 20 мм в проекцию проёма окна — это не нарушение, принято автором 05.10.2026 (вопрос К-16 закрыт). Вместе с окном изменились: направление паркета в Детской 2 (по оси X → по оси Y, вдоль света от окна), портьеры и римская штора T16, T17 (длина, карниз). Декор: спатифиллум ДК16 перенесён с (9900; 6100) на (10200; 4300), основание в данных не записано. Окно, стол M_35, кресло M_36, стеллаж M_37, портьеры T16, T17, декор ДК16 и направление паркета помечены знаком предложения.	Утверждено: Кырлан А.С., автор проекта, 05.10.2026 — утверждены положение и размеры мебели «Детской 2»: стол M_35 1400 × 650 (заход края стола на 20 мм в проекцию проёма окна принят), кресло M_36, стеллаж M_37 1200 × 2100. Не утверждены (допущение или предложение): положение окна, портьеры T16 и T17, декор ДК16, направление паркета. Предложил: решение автора проекта, оформлено исполнителем по его поручению (запись внесена конвейером).
ИЗ-2	05.10.2026	л. 43 — План розеток и электровыводов л. 45 — План освещения л. 47 — Управление светильниками л. 46 — Техническое задание на подбор светильников	Детская 2: общий свет L15 (шесть спотов), выключатель S14 (L15 и свет санузла). Бра и отдельных линий у кровати и у стола не было.	Добавлены: бра Св63 у изголовья кровати M_33 (стена А, смещение 510, высота 1400 мм, 6 Вт, 2700 K, линия L21) и выключатель S17 (стена А, смещение 1050, высота 900 мм); бра Св67 над рабочим столом M_35 (стена Б, смещение 2200, высота 1300 мм, 7 Вт, 3000 K, линия L22) и выключатель S18 (стена Б, смещение 1410, высота 900 мм). S18 стоял на смещении 1350 мм и оказывался за стеллажом M_37 1200×2100: стеллаж возвращён к прежнему размеру, выключатель перенесён в просвет между стеллажом и столом. Заказчик бра не заказывал, основание в данных не записано; позиции помечены как предложение проектировщика.	Утверждено: Кырлан А.С., автор проекта, 05.10.2026 — утверждён перенос выключателя S18 в просвет между стеллажом M_37 и столом M_35 (стеллаж прежнего размера 1200 × 2100). Не утверждены (предложение проектировщика): бра Св63 и Св67, выключатели S17 и S18 как позиции, линии L21 и L22. Предложил: решение автора проекта, оформлено исполнителем по его поручению (запись внесена конвейером).
ИЗ-3	05.10.2026	л. 45 — План освещения л. 46 — Техническое задание на подбор светильников	Санузел: общий свет L12 (спот Св51), света у зеркала не было.	Добавлен светильник Св64 над зеркалом ДК17 (стена Б, смещение 600, высота 1950 мм, 8 Вт, 3000 K, IP44, драйвер встроен, линия L12, группа 4). Основание: (свет у зеркала в санузле). Заказчик светильник не заказывал; решение исполнителя, знак «**» у Св64 остаётся.	Утверждено: исполнитель по поручению Кырлана А.С., 05.10.2026. Предложил: исполнитель.

					Проект: Четырёхкомнатная квартира		
	Лист	№ док.	Подпись	Дата	Открытые вопросы, принятые допущения и конфликты. Лист 3 из 5	Стадия	Лист	Листов
Дизайнер	Кырлан А.С.			04.11.26		П	94	120

Изменения проекта после выпуска листов (реестр изменений) (продолжение)

№	Дата	Лист	Было	Стало	Кто решил, подпись
ИЗ-4	05.10.2026	л. 47 — Управление светильниками л. 46 — Техническое задание на подбор светильников	Зал: выключатель S2 (лента в карнизе L3) без светорегулятора, сценариев света нет.	В S2 добавлен светорегулятор (тип TE, под диммируемую ленту); записаны четыре сценария света: «Вечер» (L1 0 %, L2 100 %, L3 50 %), «Гости» (100/100/100 %), «Кино» (0/0/20 %), «Уборка» (100/100/0 %). Основание: (гостиная с тремя и более группами света — сценарий; в Зале L1–L3) и (промежуточный уровень — группе на светорегуляторе). Уровни выбрал исполнитель, заказчик их не задавал; знак «**» у S2 остаётся. Сценарии и диммер записаны для Зала; в Гостиной их нет.	Утверждено: исполнитель по поручению Кырлана А.С., 05.10.2026. Предложил: исполнитель.
ИЗ-5	05.10.2026	л. 41, 42 — Однолинейная схема щита л. 43 — План розеток и электровыводов полный альбом	Розетки Гостиной Р36–Р38 — в группе 9 «розетки фартука кухни». Щит ЩРВ-П-54 на 54 модуля, занято 42.	Новая группа 19 «розетки гостиной»: автомат С16, УЗО 30 мА типа А, кабель ВВГнг(А)-LS 3×2,5, 1,0 кВт, длина линии 30 м (оценка, не замер). Щит ЩРВ-П-72 на 72 модуля, занято 44. Основание щита: при 44 занятых модулях резерв ЩРВ-П-54 составил бы 10 модулей (18,5 %) — меньше 20 %. Основание группы 19: (не больше 12 гнёзд на группу 2,5 мм²; практика): с Р36–Р38 в группе 9 было бы 14 гнёзд, осталось 8. Знак «**» у щита и Р36–Р38 остаётся.	Не утверждено: подписи нет. решение исполнителя; на утверждение А. С. Кырлана
ИЗ-6	05.10.2026	л. 34 — План размещения дверей л. 16 — План размещения мебели и оборудования	Гардеробная 1: дверь в Гостиную, проём 1420 мм по скану, полотно распашное 1420 мм.	Полотно раздвижное, две створки по 710 мм по накладной направляющей; проём 1420 мм прежний. Основание: распашное полотно 1420 мм в помещении 1400×2230 задевало стеллаж M_38. Заказчик замену не заказывал; решение исполнителя, знак предложения у двери остаётся.	Утверждено: исполнитель по поручению Кырлана А.С., 05.10.2026. Предложил: исполнитель.
ИЗ-7	05.10.2026	полный альбом л. 14, 15 — Колерная карта л. 45 — План освещения л. 47 — Управление светильниками	Гостиная: акцентная стена А в L481 (finish.accent); предметов декора и подсветки картины не было; выключатель S16 одноклавишный (L19).	Конвейер заменял акцентную стену предметами и ради порога снял её; решением от 05.10.2026 акцентная стена А возвращена (доля 16 % выше порога 15 %, замечание открыто, К-7). Предметы оставлены как предложение: картина ДК20 (стена Г, 800×600), ваза ДК21, подсветка картины Св65, Св66 (линия L20), вторая клавиша S16, подсветка помечена как предложение проектировщика. Нужны ли предметы при акцентной стене — решает автор.	Не утверждено: подписи нет. ИИ-конвейер, на утверждение А. С. Кырлана
ИЗ-8	05.10.2026	л. 6 — План планировки от заказчика л. 43 — План розеток и электровыводов л. 45 — План освещения	Наружный контур: ступени по осям 14780, 7710, 6540, 7970 мм. Прихожая-коридор: розетка Р27 на стене Г, смещение 1990; ИП5 (5600; 3800). Коридор: ИП3 (8500; 3200), выключатель S4 смещение 870. Детская 1: Св20, Св25 по X 14450. Ванная: Св13 по X 7700, дверь смещение 100. Детская 2: Р33 смещение 3140 мм.	Ступени контура 14840, 7770, 6600, 8030 мм (+60 мм): приведены к крайним граням помещений модели (Детская 1, Санузел); после этого окна Гостиной, Детской 1 и Детской 2 лежат на гранях контура. Р27 на стене А, смещение 1750; ИП5 (5500; 4400), ИП3 (8300; 2850). Св20, Св25 по X 14400 и Св13 по X 7600. Дверь ванной смещение 110. Р33 на смещении 1100 мм: прежнее место попало в проём перенесённого окна (ИЗ-1). S4 смещение 880: вслед за дверью ванной (110 вместо 100), зазор от откоса до выключателя прежний, 70 мм. Сдвиги — решение исполнителя; знак «**» у сдвинутых позиций остаётся.	Не утверждено: подписи нет. решение исполнителя; на утверждение А. С. Кырлана
ИЗ-9	05.10.2026	л. 43 — План розеток и электровыводов л. 45 — План освещения л. 6 — План планировки от заказчика	Слаботочные точки (5 шт.) без слаботочного щита; точек доступа Wi-Fi не было; параметров щита ЩС в данные проекта не было.	Добавлены: слаботочный щит ЩС (Прихожая-коридор, стена А, смещение 1380, высота 1600 мм), точки доступа AP1 (5500; 5000) и AP2 (13000; 4300), кабель U/UTP кат. 6 у LAN4 и в данные проекта, щит ЩС: глубина 150 мм, пластик, вентилируемый, роутер внутри. Основание: (нет щита) и (ориентир две точки доступа на 102 м²). Заказчик слаботочку в таком составе не заказывал; решение исполнителя, знак «**» у ЩС, AP1, AP2 и LAN4 остаётся. Две точки Wi-Fi и тип щита автор не выбирал.	Не утверждено: подписи нет. решение исполнителя; на утверждение А. С. Кырлана
ИЗ-10	05.10.2026	л. 43 — План розеток и электровыводов полный альбом	Кухня: розетка Р21 (вытяжка M_24) на высоте 2200 мм, решение, назначение «вытяжка M_24».	Назначение «вытяжка M_24 (в модуле, съёмная панель)» и признак доступа access: true. Высота 2200 мм прежняя, знак предложения прежний, флаг «решение» снят: решающего нет; высота автором не подтверждена, вопрос К-23.	Не утверждено: подписи нет. решение исполнителя; на утверждение А. С. Кырлана
ИЗ-11	05.10.2026	л. 16 — План размещения мебели и оборудования л. 14, 15 — Колерная карта	Марки декора Д1…Д19 (совпадали с префиксом дверей Д). Образцов колерной карты 10.	Марки декора ДК1…ДК19, позиции не менялись. Добавлен образец № 11 (J484, Tikkurila): отдельный выкрас плинтуса коридора и прихожей на МДФ.	Не утверждено: подписи нет. решение исполнителя; на утверждение А. С. Кырлана
ИЗ-12	24.09.2026	л. 43 — План розеток и электровыводов полный альбом	В ванной комнате и санузле не было вывода к вентилятору вытяжки и коробки уравнивания потенциалов.	Добавлены выводы к вентиляторам: ЭВ2 (ВР1, ванная комната) и ЭВ5 (ВР3, санузел) — группа 4, высота 2550 мм, IP44, включение с основным светом, таймер выбега в вентиляторе; коробки уравнивания потенциалов КУП1 (ванная комната) и КУП2 (санузел) — высота 300 мм, у входа, вне зон 0–2. Основание: правила проверки (питание вентилятора вытяжки мокрого помещения) и (КУП в помещении с ванной или душем). Заказчик эти позиции не заказывал; решение исполнителя, ЭВ2, ЭВ5, КУП1 и КУП2 со знаком «**».	Утверждено: исполнитель по поручению Кырлана А.С., 05.10.2026. Предложил: исполнитель.
ИЗ-13	05.10.2026	л. 16 — План размещения мебели и оборудования л. 6 — План планировки от заказчика	Общая комната квартиры не названа: «Зал» (18,16 м²) или «Гостиная» (14,55 м²); если бы общей считалась «Гостиная», норма 16 м² не выполнялась (вопрос К-9).	Общей комнатой назначен «Зал» (18,16 м²): он больше «Гостиной», проходит норму общей комнаты не менее 16 м² (СП 54.13330.2022, п. 5.11) и по концепции интерьера несёт обеденную группу на шесть персон. «Гостиная» (14,55 м²) остаётся второй жилой комнатой: для неё действует норма спальни 8 м², она выполнена. Названия и номера помещений со сканом по-прежнему не сверены (К-21).	Утверждено: Кырлан А.С., автор проекта, 05.10.2026. Предложил: решение автора проекта, оформлено исполнителем по его поручению.

					Проект: Четырёхкомнатная квартира
	Лист	№ док.	Подпись	Дата	Открытые вопросы, принятые допущения и конфликты. Лист 4 из 5
Дизайнер	Кырлан А.С.			04.11.26	

Стадия	Лист	Листов
П	95	120

Изменения проекта после выпуска листов (реестр изменений) (продолжение)

№	Дата	Лист	Было	Стало	Кто решил, подпись
ИЗ-14	05.10.2026	л. 6 — План планировки от заказчика л. 34 — План размещения дверей	Санузел (поз. 10) в эркере соединён только с «Детской 2»: другого входа нет; вход в помещение с унитазом из жилой комнаты расходится с требованием СП 54 (вопрос К-2).	Сохраняется существующее положение: вход в санузел — из «Детской 2», перепланировка с тамбуром не выполняется. Основание: требование СП 54.13330.2022 (формулировка не сверена с первоисточником) не допускает устраивать вход в помещение с унитазом из жилой комнаты; проект нового входа не устраивает, а оставляет существующий. Тамбур отнял бы площадь «Детской 2», а стены до технического заключения считаются несущими (К-3). Существующий вход взят с обмерного скана заказчика, на объекте не проверен (К-21). Это отступление от требования, рассчитанного на новое строительство, принято как существующее положение; проверка по этому пункту остаётся замечанием.	Утверждено: Кырлан А.С., автор проекта, 05.10.2026. Предложил: решение автора проекта, оформлено исполнителем по его поручению.
ИЗ-15	05.10.2026	л. 14, 15 — Колерная карта л. 16 — План размещения мебели и оборудования	Зал: акцентная стена А (ТВ-стена, L481) занимает 18 % площади поверхностей при пороге акцента 15 % (вопрос К-7).	Доля акцента 18 % принята: ТВ-стена А красится в L481 целиком, это замысел автора, на предметы акцент не переносится. Порог 15 % практики 60/30/10 превышен сознательно. Акцентная стена «Гостиной» (16 %) этим решением не затронута — вопрос К-7.	Утверждено: Кырлан А.С., автор проекта, 05.10.2026. Предложил: решение автора проекта, оформлено исполнителем по его поручению.
ИЗ-16	05.10.2026	л. 3 — Список листов	Состав выдачи не подтверждён: разделы пожарного инженера, акустика, технадзора, слаботочки и допуск ГИПа в сводке ролей числились не сданными (вопрос К-11).	Пожарный инженер, акустик и технадзор в заказ частного ремонта квартиры не входят: роли отмечены в сводке ролей пропущенными, с причиной. Слаботочка входит в состав: выпущен лист «План слаботочных сетей»; отдельная ведомость слаботочки (кабельный журнал, состав слаботочного щита) ролью не сдана и остаётся в таблице несданных разделов. Функции ГИП выполняет автор проекта, графа «ГИП» основной надписи заполнена его фамилией; членство в СРО не проверялось.	Утверждено: Кырлан А.С., автор проекта, 05.10.2026. Предложил: решение автора проекта, оформлено исполнителем по его поручению.
ИЗ-17	05.10.2026	л. 3 — Список листов	Матрицы ответственности (делает / поставляет / принимает / хранит) нет; кто покупает и кто монтирует — не определено (вопрос К-12).	Принята типовая схема частного ремонта: материалы и оборудование покупает заказчик по спецификациям проекта; монтаж ведёт подрядная бригада; приёмку скрытых работ ведёт автор проекта. Распределение закреплено по радиаторам, подоконникам, дверям, розеткам и выключателям, сантехническим приборам, светильникам и отделочным материалам. Схема уточняется договором подряда; состав подрядчиков и поставщиков остаётся вопросом К-12.	Утверждено: Кырлан А.С., автор проекта, 05.10.2026. Предложил: решение автора проекта, оформлено исполнителем по его поручению.
ИЗ-18	05.10.2026	л. 3 — Список листов	Графы «Пров.» и «Н. контр.» основной надписи пусты (вопрос К-8); как с ними поступать — не записано.	Графы «Пров.» и «Н. контр.» остаются пустыми: независимой проверки и нормоконтроля проекта не было, автор проекта сам себе их не подписывает. Комплект выпускается предварительным: пока нет подписи проверяющего и нормоконтролёра, отличных от разработчика, он не считается окончательным.	Утверждено: Кырлан А.С., автор проекта, 05.10.2026. Предложил: решение автора проекта, оформлено исполнителем по его поручению.
ИЗ-19	05.10.2026	л. 43 — План розеток и электровыводов полный альбом	Розетки ванной Р7 (стиральная машина) и Р8 (фен): по ПУЭ допустимы в зоне 3 через УЗО 30 мА, по британской норме BS 7671 (п. 701.512.3) — дальше 2,5 м от границы зоны 1; какая норма принята — вопрос К-6.	Принята норма ПУЭ (п. 7.1.48): розетки в зоне 3 помещения с ванной допустимы при защите УЗО 30 мА. Положение розеток не менялось. Основание: розетки вне зон 0–2 (до границы зоны 1: Р7 1630 мм, Р8 — 1441 мм), исполнение IP44, группы 14 и 15 защищены УЗО 30 мА типа А. Это сознательное отступление от зарубежной нормы BS 7671: в России она не действует, по ней в таком месте допустима только бритвенная розетка с разделительным трансформатором. Расстояние Р7 до угла (72 мм при норме от 150 мм) этим решением не затронуто — вопрос К-6.	Утверждено: Кырлан А.С., автор проекта, 05.10.2026. Предложил: решение автора проекта, оформлено исполнителем по его поручению.
ИЗ-20	30.10.2026	л. 34 — План размещения дверей л. 74 — Развёртки стен А, Б. Прихожая-коридор (пом. 7) л. 16 — План размещения мебели и оборудования	Проём коридор → прихожая-коридор (стена В коридора, offset 500) выходил за общую стену: на развёртке стены А прихожей видны 770 из 900 мм. Шкаф-купе М_28 (1700) заканчивался в 60 мм от проёма двери детской 2.	Проём — offset 300 (целиком в общей стене, знак «*»: положение со скана, К-21). М_28 — 1600 мм, зазор до проёма 160 мм под наличник. Вход в гостиную — вопрос К-31 с заданием на обследование.	Не утверждено: подписи нет. решение исполнителя; предложение проектировщика, на утверждение А. С. Кырлана

Разделы, не сданные к выпуску (сводка ролей)


№	Раздел	Состояние	Причина
1	Инженер слаботочки и умного дома	Не сдан	слаботочка входит в состав заказа (ИЗ-16); выпущен лист «План слаботочных сетей» (раздел электрика); отдельная ведомость слаботочки — кабельный журнал, состав слаботочного щита — не выпущена

Примечания


1. Номера листов — по ведомости рабочих чертежей комплекта (лист «Общие данные»).
2. Графа «Если решения нет» показывает состояние решения на листах; влияние на сроки и стоимость по пунктам не оценивалось.
3. Пункт, по которому принято решение, при следующем выпуске комплекта из таблиц исключается.

					Проект: Четырёхкомнатная квартира		
	Лист	№ док.	Подпись	Дата	Открытые вопросы, принятые допущения и конфликты. Лист 5 из 5	Стадия	Лист	Листов
Дизайнер	Кырлан А.С.			04.11.26		П	96	120


Общий вид

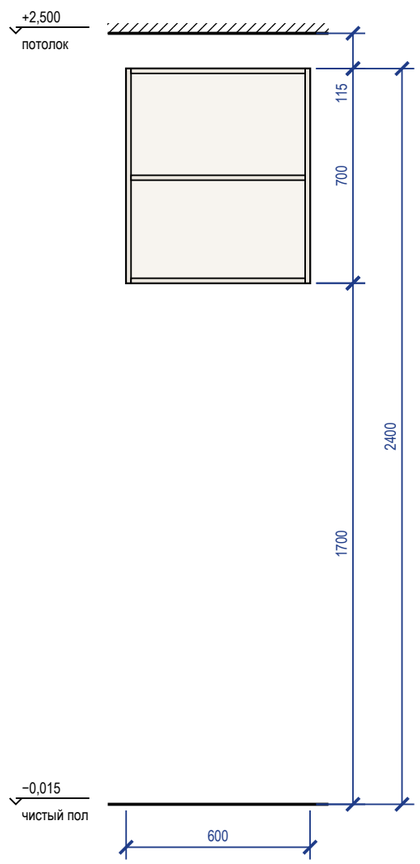

Наполнение, размеры в свету

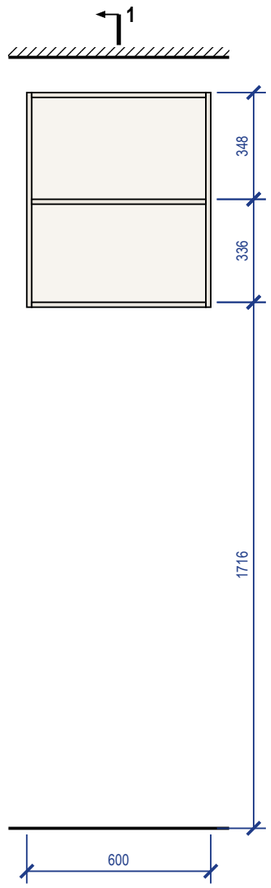


Разрез 1-1

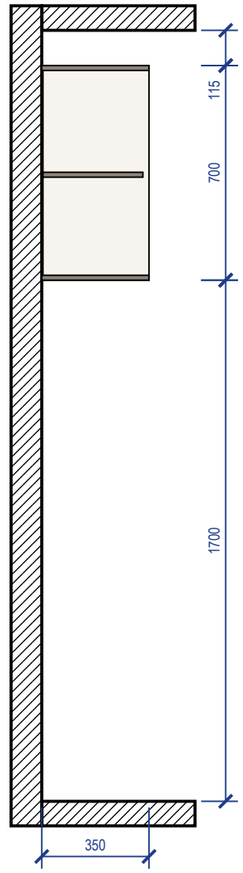

Примечания


1. Размеры — в мм по чистовой отделке; изделие 600×350×700 (Ш×Г×В). Перед раскроем — контрольный замер цеха после чистовой отделки стен, пола и потолка.
2. Корпус — ЛДСП 16 мм, задняя стенка ХДФ 4 мм в паз, навесной корпус без цоколя, низ на 1700 мм от чистого пола; открытая система: без фасадов.
3. Кромка: скрытые торцы 0,4 мм, видимые 2 мм (ПВХ/АБС).
4. Присадка по 32-й системе — выполняет цех.
5. Зазор до потолка 115 мм — закрыть планкой в цвет корпуса при монтаже.
6. Навесной корпус — на стене: крепление к стене, 2 точки; основание стены и шаг анкеров — монтажная схема шкафов.

3D орто

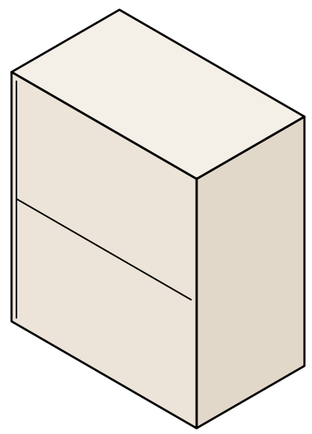


					Проект: Четырёхкомнатная квартира		**М 1:20**
	Лист	№ док.	Подпись	Дата	Система хранения М_07	Стадия	Лист	Листов
Дизайнер	Кырлан А.С.			04.11.26		П	Д_1	120


Общий вид

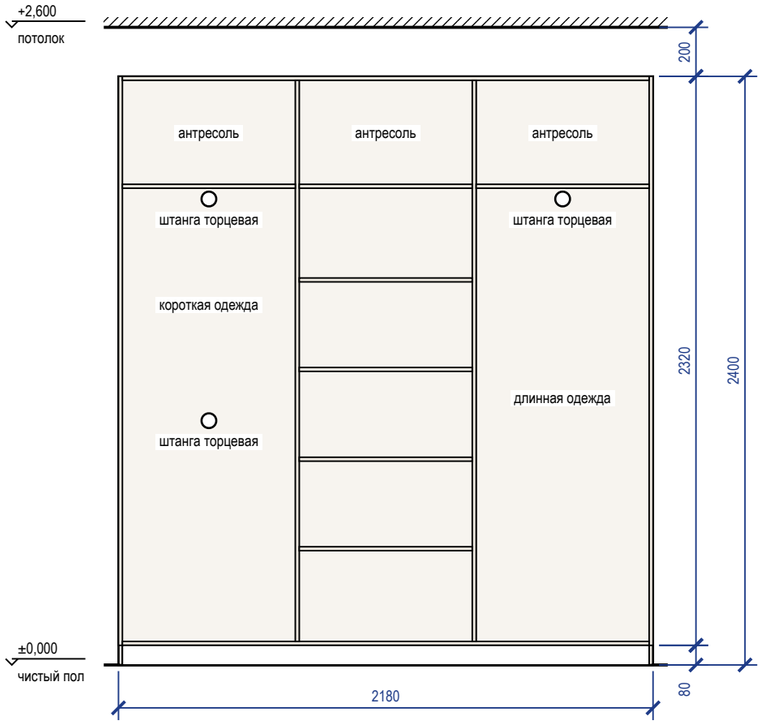


Наполнение, размеры в свету

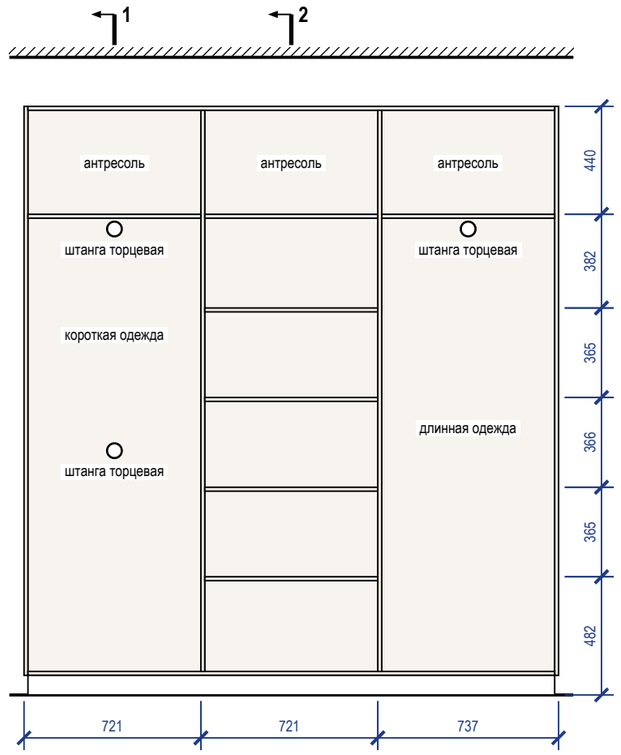

Разрез 1-1

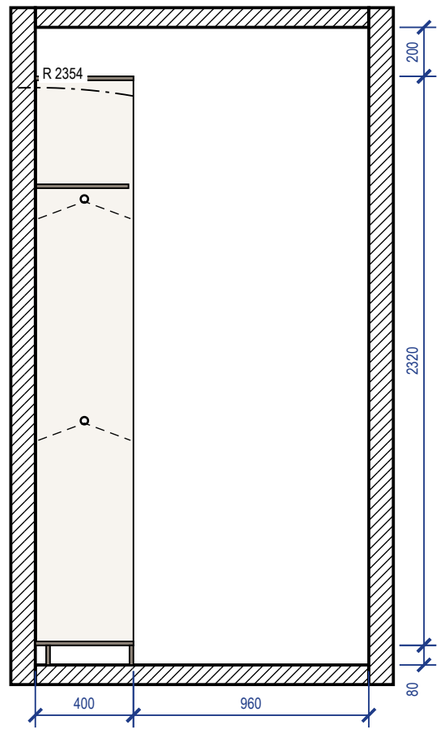


Разрез 2-2

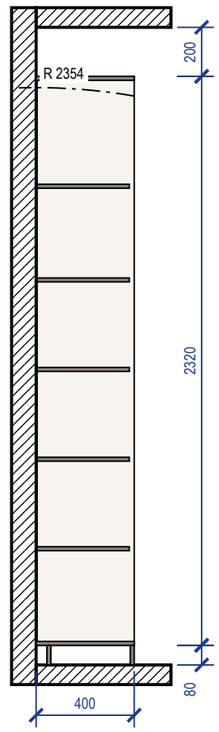

Примечания


1. Размеры — в мм по чистовой отделке; изделие 2180×400×2400 (Ш×Г×В). Перед раскроем — контрольный замер цеха после чистовой отделки стен, пола и потолка.
2. Корпус — ЛДСП 16 мм, задняя стенка ХДФ 4 мм в паз, цоколь 80 мм на регулируемых опорах; открытая система: без фасадов.
3. Кромка: скрытые торцы 0,4 мм, видимые 2 мм (ПВХ/АБС).
4. Присадка по 32-й системе — выполняет цех.
5. Зазор до потолка 200 мм.
6. Подъём корпуса: диагональ боковины без цоколя √(2320² + 400²) = 2354 мм < 2600 мм до потолка — корпус собирается лёжа, поднимается поворотом и ставится на цоколь.
7. Крепление к стене от опрокидывания: крепление к стене, 4 точки; основание стены и шаг анкеров — монтажная схема шкафов.
8. Проход перед изделием 960 мм показан на разрезе 1-1.

3D орто

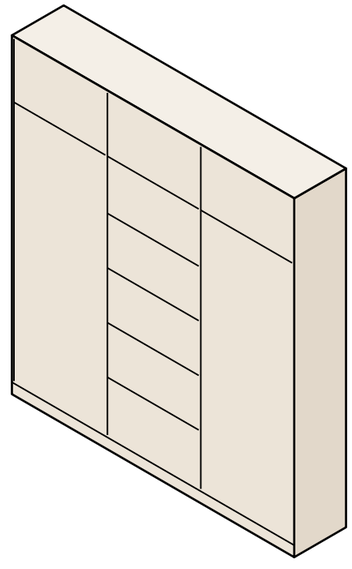


					Проект: Четырёхкомнатная квартира	**М 1:25**
	Лист	№ док.	Подпись	Дата		
Дизайнер	Кырлан А.С.			04.11.26	Система хранения М_08	Стадия: П; Лист: Д_2; Листов: 120


Общий вид

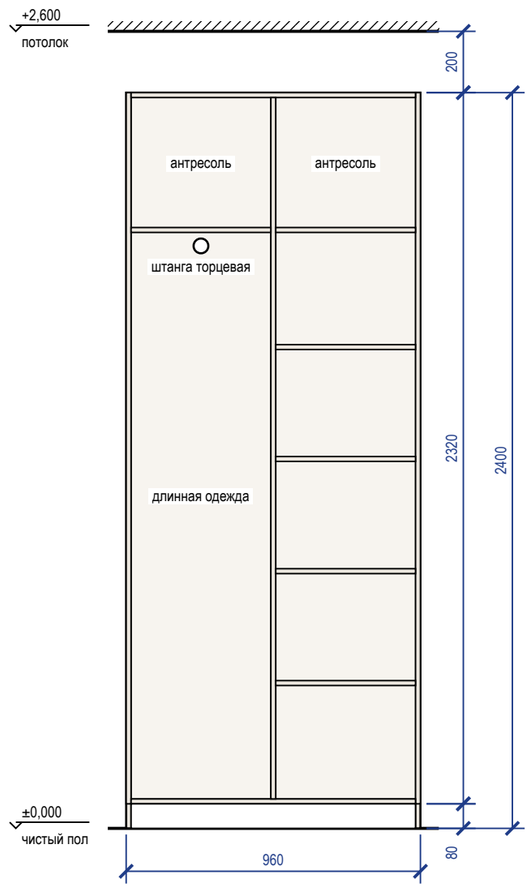


Наполнение, размеры в свету

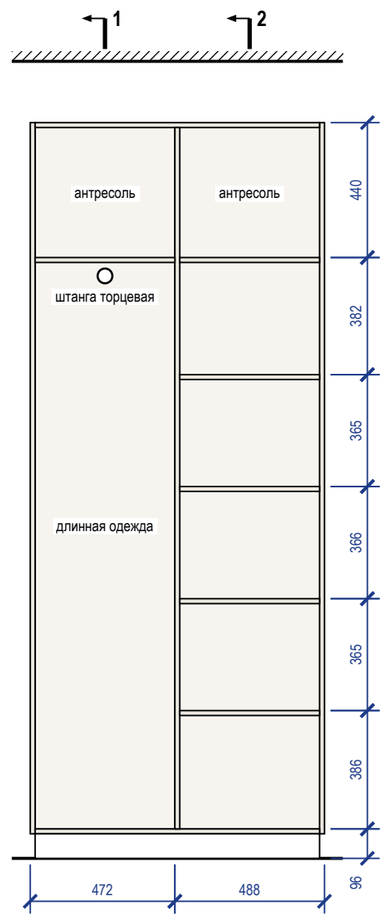

Разрез 1-1

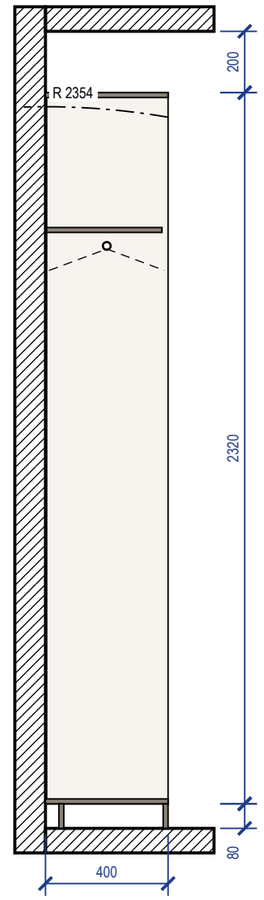


Разрез 2-2

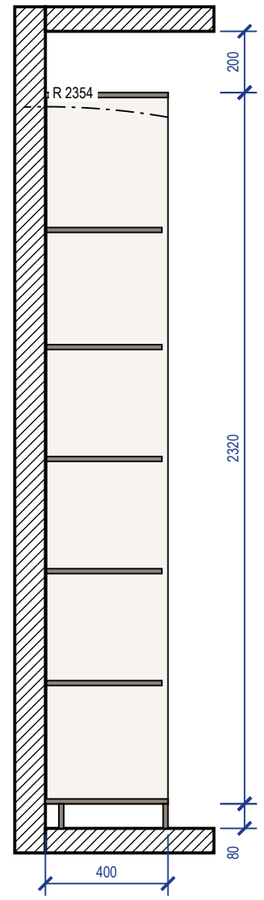

Примечания


1. Размеры — в мм по чистовой отделке; изделие 960×400×2400 (Ш×Г×В). Перед раскроем — контрольный замер цеха после чистовой отделки стен, пола и потолка.
2. Корпус — ЛДСП 16 мм, задняя стенка ХДФ 4 мм в паз, цоколь 80 мм на регулируемых опорах; открытая система: без фасадов.
3. Кромка: скрытые торцы 0,4 мм, видимые 2 мм (ПВХ/АБС).
4. Присадка по 32-й системе — выполняет цех.
5. Зазор до потолка 200 мм.
6. Подъём корпуса: диагональ боковины без цоколя $\sqrt{(2320^2 + 400^2)} = 2354$ мм < 2600 мм до потолка — корпус собирается лёжа, поднимается поворотом и ставится на цоколь.
7. Крепление к стене от опрокидывания: крепление к стене, 3 точки; основание стены и шаг анкеров — монтажная схема шкафов.

3D орто

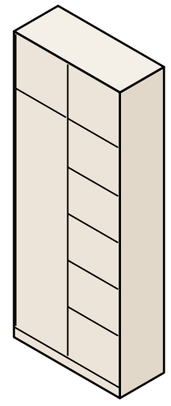


					Проект: Четырёхкомнатная квартира	**М 1:20**
	Лист	№ док.	Подпись	Дата		
Дизайнер	Кырлан А.С.			04.11.26	Система хранения М_09	Стадия: П; Лист: Д_3; Листов: 120


Вид с фасадами

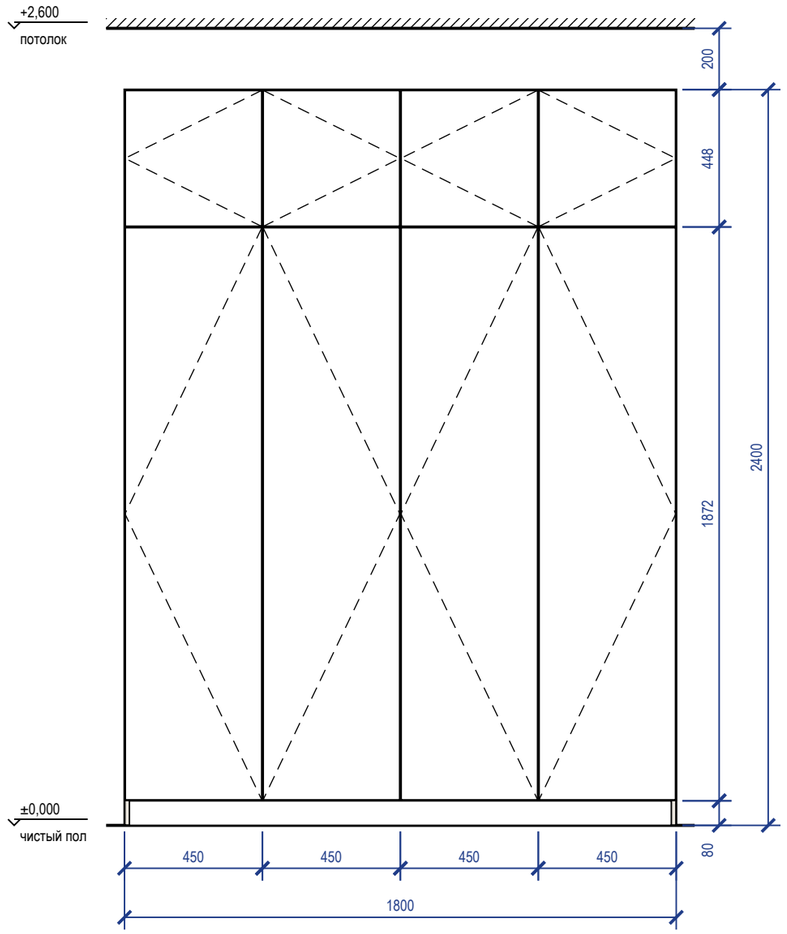


Вид без фасадов

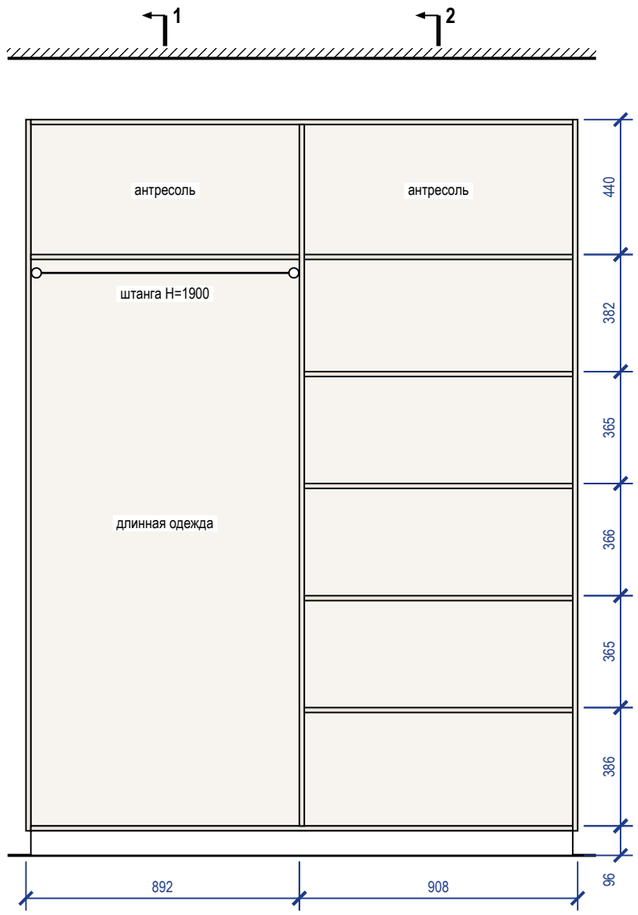

Разрез 1-1

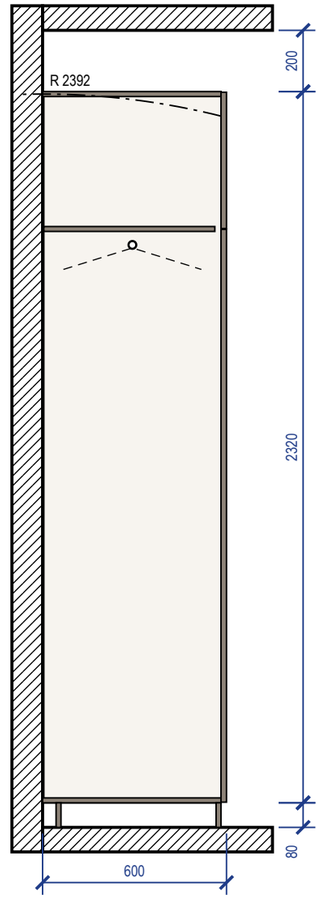


Разрез 2-2

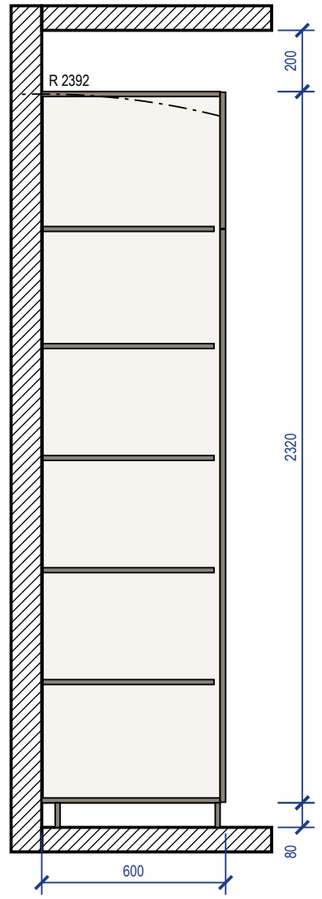

Примечания


1. Размеры — в мм по чистовой отделке; изделие 1800×600×2400 (Ш×Г×В). Перед раскроем — контрольный замер цеха после чистовой отделки стен, пола и потолка.
2. Корпус — ЛДСП 16 мм, задняя стенка ХДФ 4 мм в паз, цоколь 80 мм на регулируемых опорах; фасады накладные — МДФ 18 мм, эмаль матовая, 18 мм; цвет — по колерной карте; петли с доводчиком: фасад 1869 мм — 4 петли, фасад 445 мм — 2 петли.
3. Кромка: скрытые торцы 0,4 мм, видимые 2 мм (ПВХ/АБС).
4. Номинальные зазоры: между фасадами 3 мм, фасад — стена и фасад — потолок не менее 3 мм, фасад ящика — стойка 2 мм.
5. Присадка по 32-й системе — выполняет цех.
6. Зазор до потолка 200 мм.
7. Подъём корпуса: диагональ боковины без цоколя $\sqrt{(2320^2 + 582^2)} = 2392$ мм < 2600 мм до потолка — корпус собирается лёжа, поднимается поворотом и ставится на цоколь.
8. Крепление к стене от опрокидывания: уголок к стене, 3 шт.; основание стены и шаг анкеров — монтажная схема шкафов.

3D орто

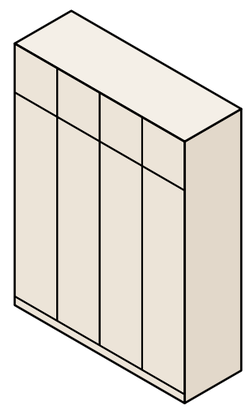


					Проект: Четырёхкомнатная квартира	**М 1:20**
	Лист	№ док.	Подпись	Дата		
Дизайнер	Кырлан А.С.			04.11.26	Шкаф распашной М_15	Стадия: П; Лист: Д_4; Листов: 120


Общий вид

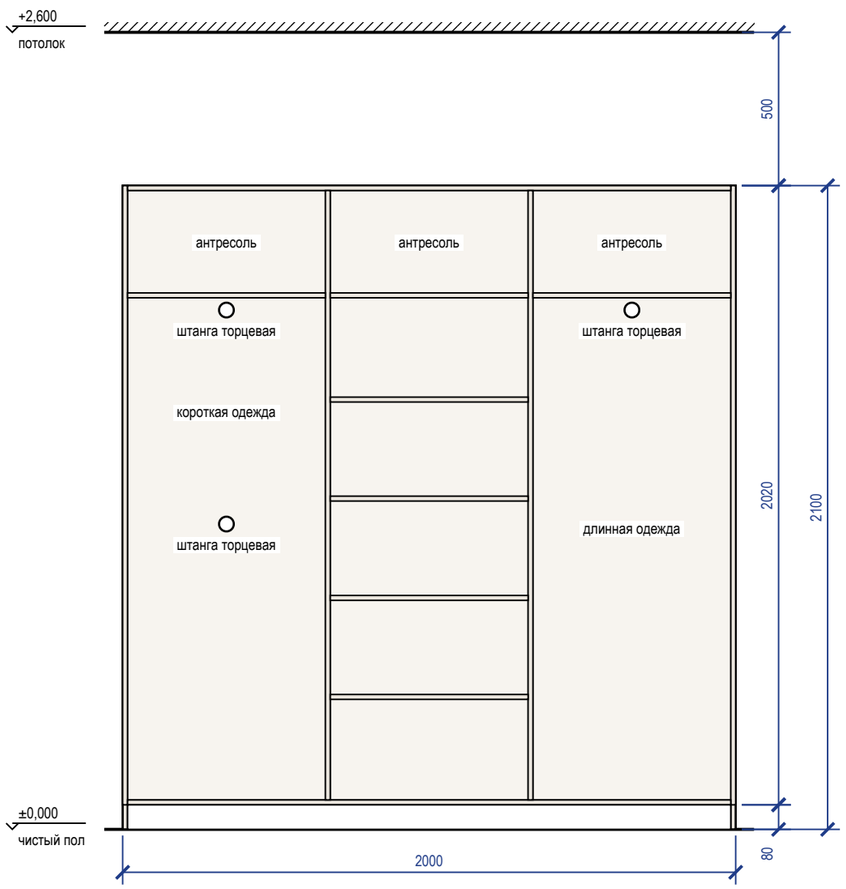


Наполнение, размеры в свету

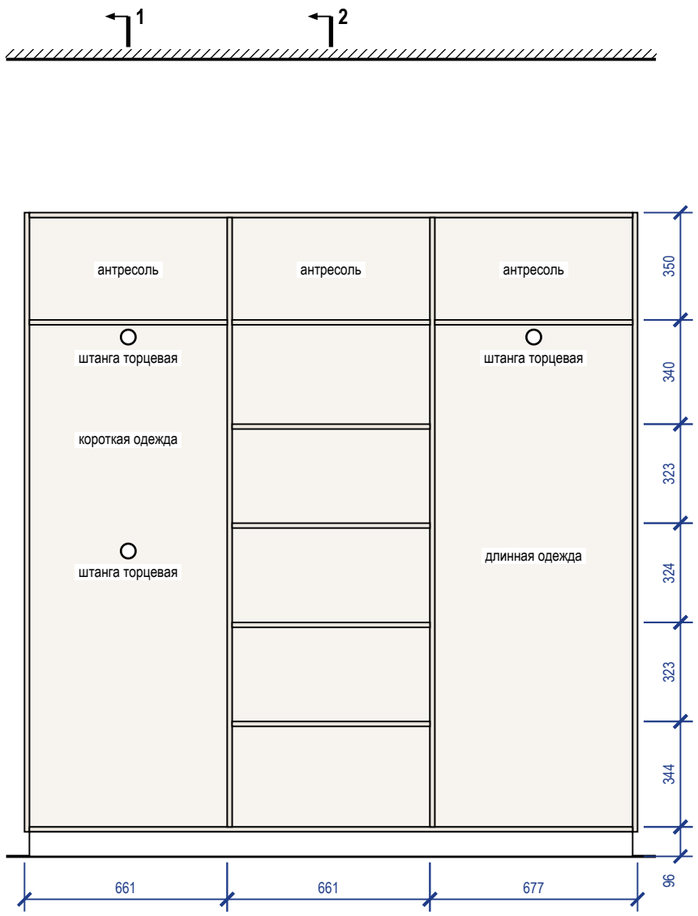

Разрез 1-1

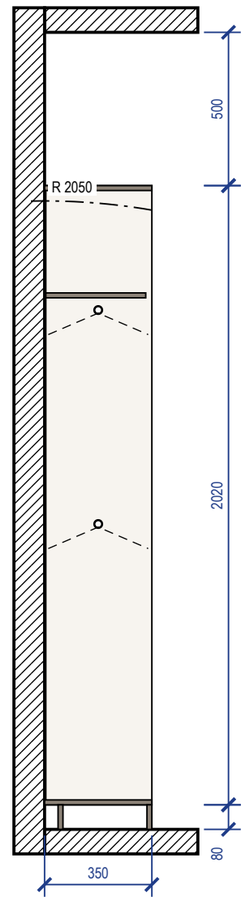


Разрез 2-2

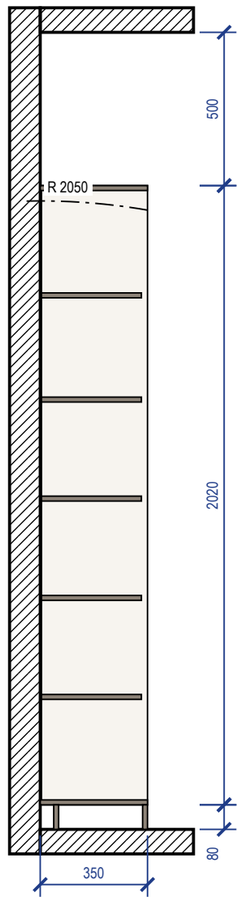

Примечания


1. Размеры — в мм по чистовой отделке; изделие 2000×350×2100 (Ш×Г×В). Перед раскроем — контрольный замер цеха после чистовой отделки стен, пола и потолка.
2. Корпус — ЛДСП 16 мм, задняя стенка ХДФ 4 мм в паз, цоколь 80 мм на регулируемых опорах; открытая система: без фасадов.
3. Кромка: скрытые торцы 0,4 мм, видимые 2 мм (ПВХ/АБС).
4. Присадка по 32-й системе — выполняет цех.
5. Зазор до потолка 500 мм.
6. Подъём корпуса: диагональ боковины без цоколя $\sqrt{(2020^2 + 350^2)} = 2050$ мм < 2600 мм до потолка — корпус собирается лёжа, поднимается поворотом и ставится на цоколь.
7. Крепление к стене от опрокидывания: крепление к стене, 3 точки; основание стены и шаг анкеров — монтажная схема шкафов.

3D орто

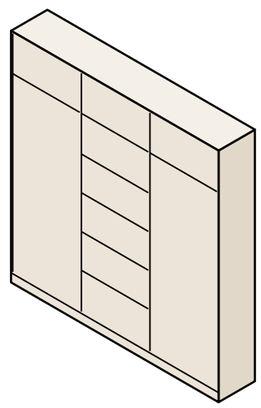


					Проект: Четырёхкомнатная квартира	**М 1:20**
	Лист	№ док.	Подпись	Дата		
Дизайнер	Кырлан А.С.			04.11.26	Система хранения М_17	Стадия / Лист / Листов
						П / Д_5 / 120


Вид с фасадами

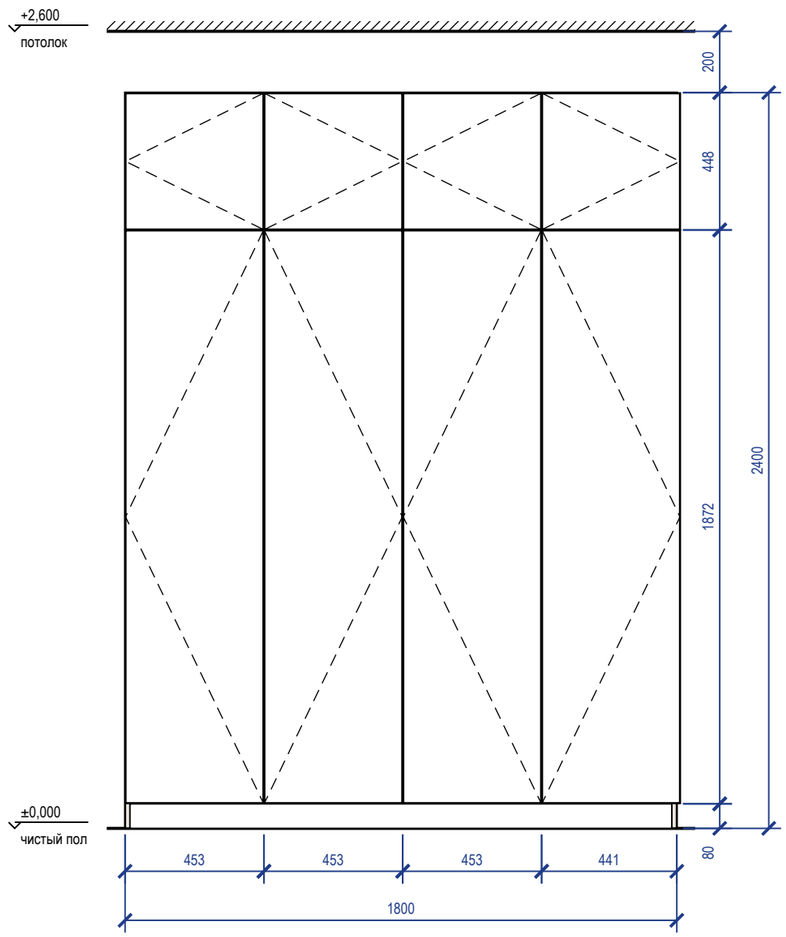

Вид без фасадов

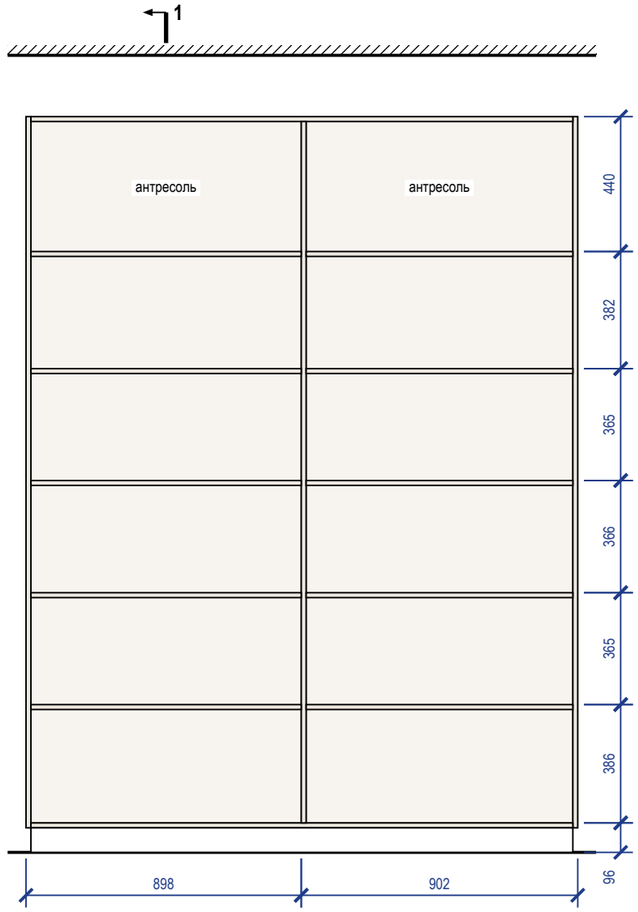


Разрез 1-1

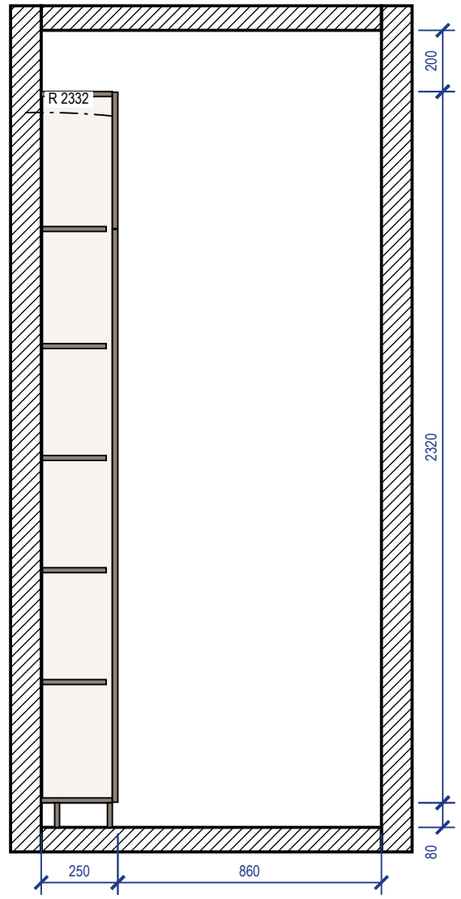

Примечания


1. Размеры — в мм по чистовой отделке; изделие 1800×250×2400 (Ш×Г×В). Перед раскроем — контрольный замер цеха после чистовой отделки стен, пола и потолка.
2. Корпус — ЛДСП 16 мм, задняя стенка ХДФ 4 мм в паз, цоколь 80 мм на регулируемых опорах; фасады накладные — МДФ 18 мм, эмаль матовая, 18 мм; цвет — по колерной карте; петли с доводчиком: фасад 1869 мм — 4 петли, фасад 445 мм — 2 петли.
3. Кромка: скрытые торцы 0,4 мм, видимые 2 мм (ПВХ/АБС).
4. Номинальные зазоры: между фасадами 3 мм, фасад — стена и фасад — потолок не менее 3 мм, фасад ящика — стойка 2 мм.
5. Присадка по 32-й системе — выполняет цех.
6. Зазор до потолка 200 мм.
7. Подъём корпуса: диагональ боковины без цоколя √(2320² + 232²) = 2332 мм < 2600 мм до потолка — корпус собирается лёжа, поднимается поворотом и ставится на цоколь.
8. Крепление к стене от опрокидывания: крепление к стене, 4 точки; основание стены и шаг анкеров — монтажная схема шкафов.
9. Проход перед изделием 860 мм показан на разрезе 1-1.

3D орто

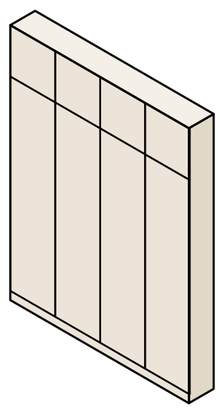


					Проект: Четырёхкомнатная квартира	**М 1:20**
	Лист	№ док.	Подпись	Дата		
Дизайнер	Кырлан А.С.			04.11.26	Система хранения М_18	Стадия: П; Лист: Д_6; Листов: 120


Вид с фасадами

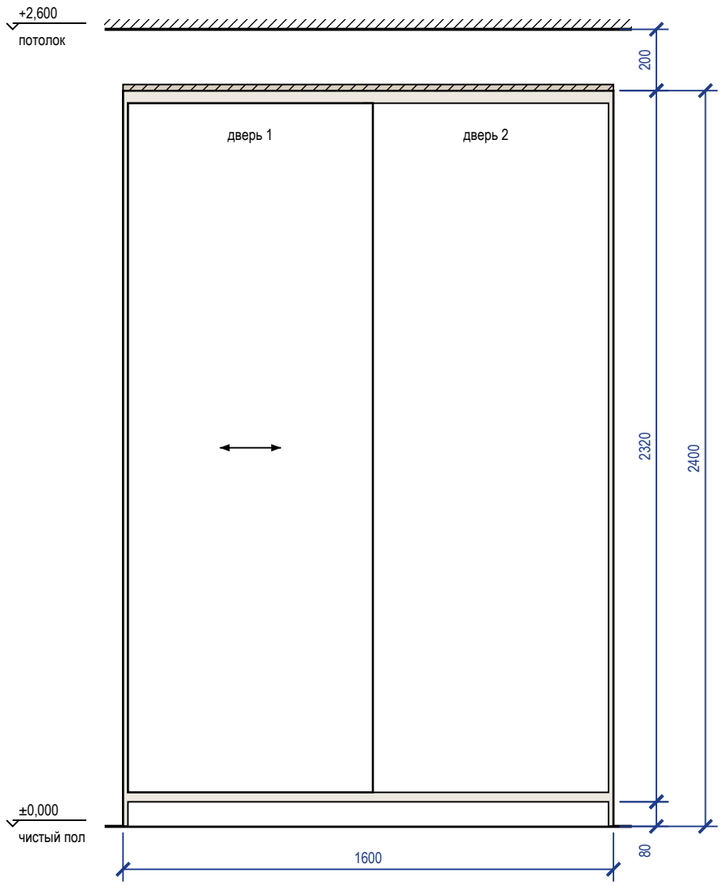


Вид без фасадов

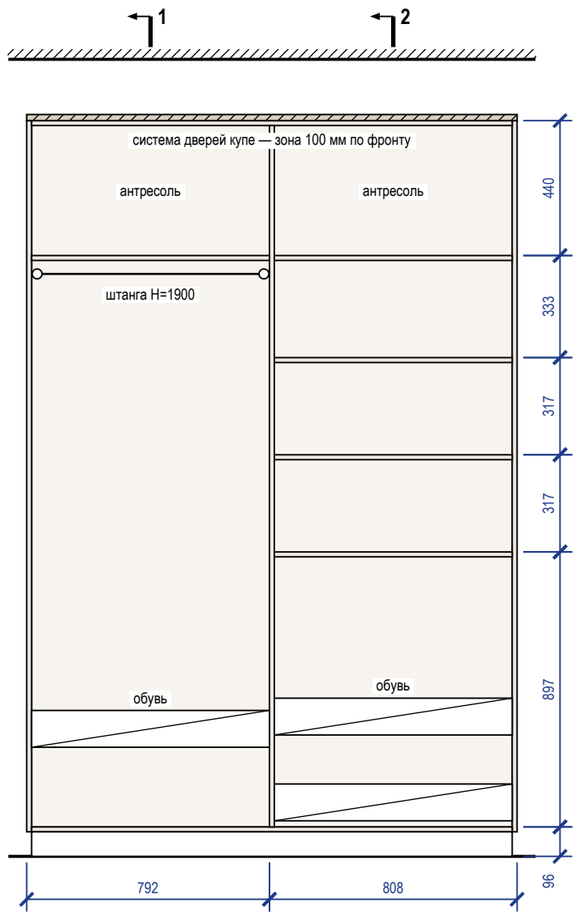

Разрез 1-1

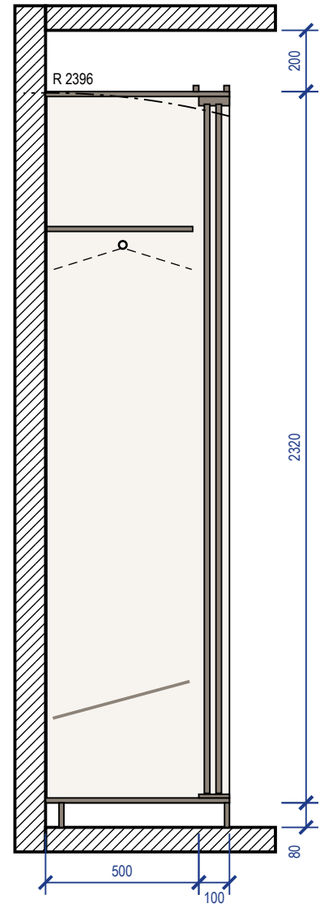


Разрез 2-2

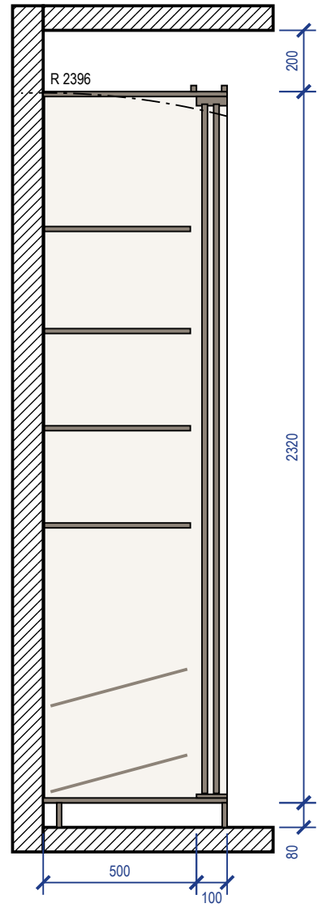

Примечания


1. Размеры — в мм по чистовой отделке; изделие 1600×600×2400 (Ш×Г×В). Перед раскроем — контрольный замер цеха после чистовой отделки стен, пола и потолка.
2. Корпус — ЛДСП 16 мм, задняя стенка ХДФ 4 мм в паз, цоколь 80 мм на регулируемых опорах; двери купе — ЛДСП 10 мм в алюминиевом профиле; нахлёст 30 мм, ширина двери 799 мм, высота — проём минус 40 мм; цвет — по колерной карте.
3. Кромка: скрытые торцы 0,4 мм, видимые 2 мм (ПВХ/АБС).
4. Номинальные зазоры: дверь купе — боковина 3 мм, фасад ящика — стойка 2 мм; ящики внутри купе — с накладкой 30 мм на стойке со стороны нахлёста дверей.
5. Присадка по 32-й системе — выполняет цех.
6. Компенсатор 20 мм — короб из ЛДСП по фронту и торцам, подгоняется к потолку при монтаже (припуск 20 мм), крепится к корпусу и к потолку.
7. Подъём корпуса: диагональ боковины без цоколя $\sqrt{(2320^2 + 600^2)} = 2396$ мм < 2600 мм до потолка — корпус собирается лёжа, поднимается поворотом и ставится на цоколь.
8. Крепление к стене от опрокидывания: крепление к стене, 3 точки; основание стены и шаг анкеров — монтажная схема шкафов.

3D орто

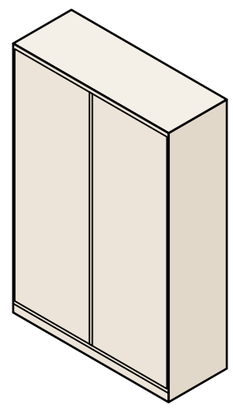


					Проект: Четырёхкомнатная квартира	**М 1:20**
	Лист	№ док.	Подпись	Дата		
Дизайнер	Кырлан А.С.			04.11.26	Шкаф-купе М_28	Стадия: П; Лист: Д_7; Листов: 120


Общий вид

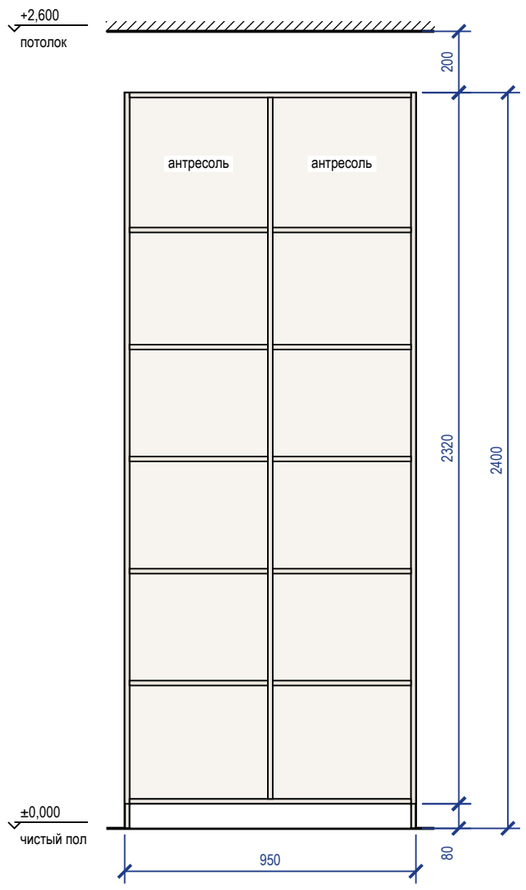

Наполнение, размеры в свету

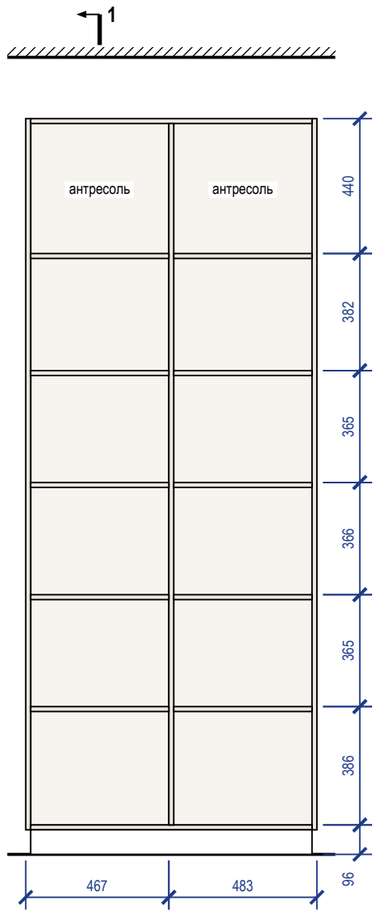


Разрез 1-1

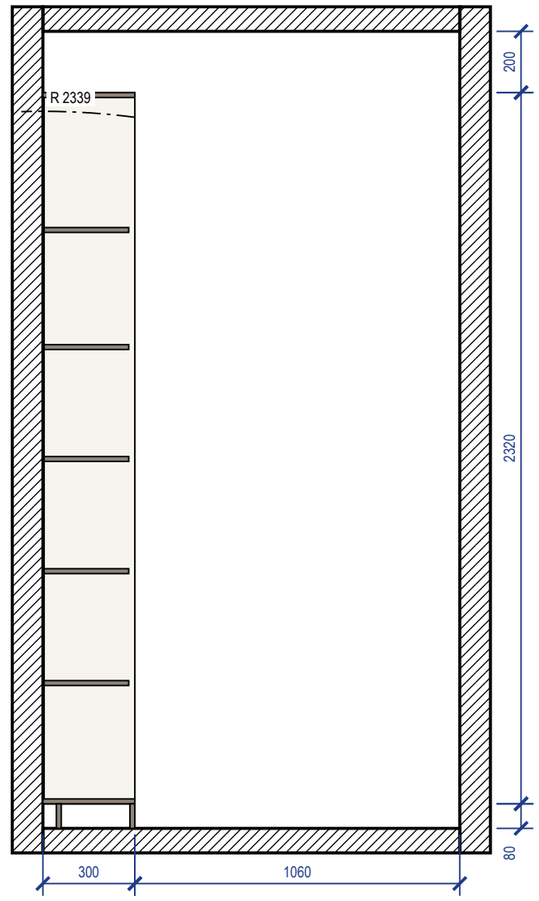

Примечания


1. Размеры — в мм по чистовой отделке; изделие 950×300×2400 (Ш×Г×В). Перед раскроем — контрольный замер цеха после чистовой отделки стен, пола и потолка.
2. Корпус — ЛДСП 16 мм, задняя стенка ХДФ 4 мм в паз, цоколь 80 мм на регулируемых опорах; открытая система: без фасадов.
3. Кромка: скрытые торцы 0,4 мм, видимые 2 мм (ПВХ/АБС).
4. Присадка по 32-й системе — выполняет цех.
5. Зазор до потолка 200 мм.
6. Подъём корпуса: диагональ боковины без цоколя $\sqrt{(2320^2 + 300^2)} = 2339$ мм < 2600 мм до потолка — корпус собирается лёжа, поднимается поворотом и ставится на цоколь.
7. Крепление к стене от опрокидывания: крепление к стене, 3 точки; основание стены и шаг анкеров — монтажная схема шкафов.
8. Проход перед изделием 1060 мм показан на разрезе 1-1.

3D орто

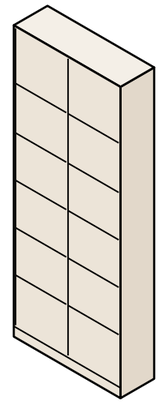


					Проект: Четырёхкомнатная квартира	**М 1:20**
	Лист	№ док.	Подпись	Дата		
Дизайнер	Кырлан А.С.			04.11.26	Система хранения М_31	Стадия: П; Лист: Д_8; Листов: 120


Общий вид

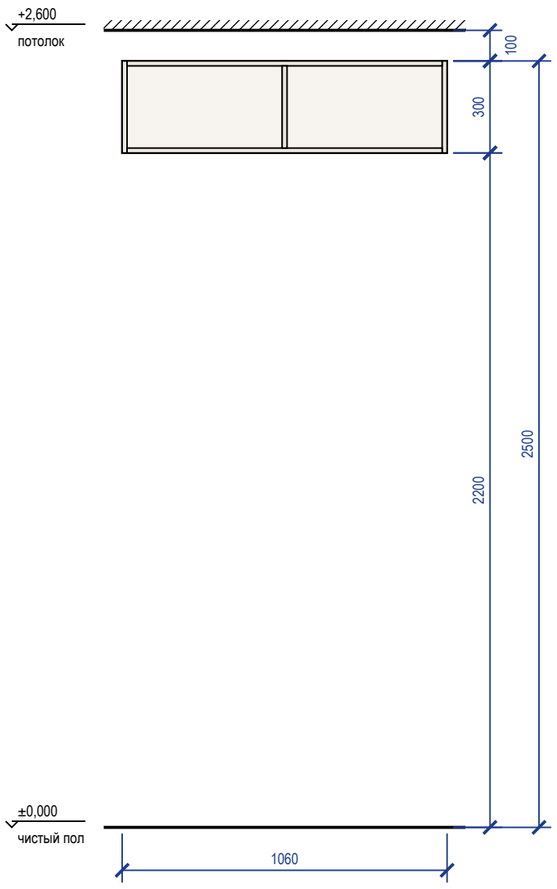

Наполнение, размеры в свету

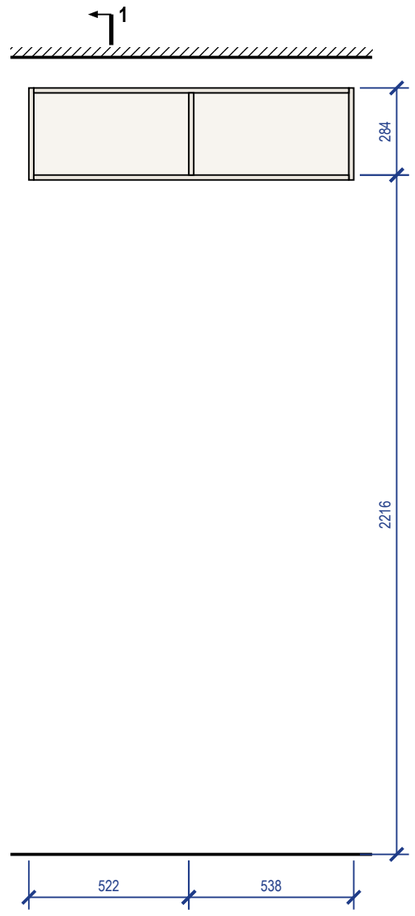


Разрез 1-1

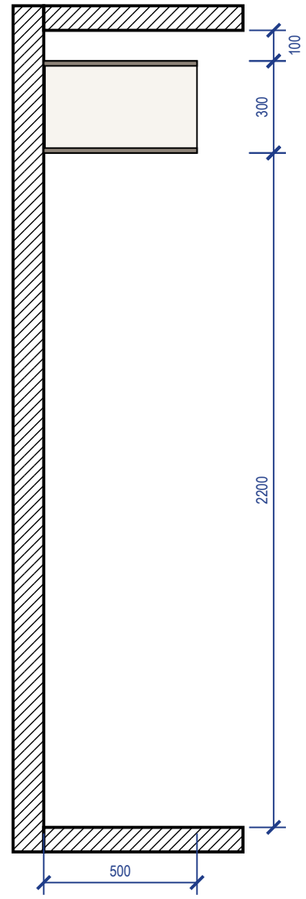

Примечания


1. Размеры — в мм по чистовой отделке; изделие 1060×500×300 (Ш×Г×В). Перед раскроем — контрольный замер цеха после чистовой отделки стен, пола и потолка.
2. Корпус — ЛДСП 16 мм, задняя стенка ХДФ 4 мм в паз, навесной корпус без цоколя, низ на 2200 мм от чистого пола; открытая система: без фасадов.
3. Кромка: скрытые торцы 0,4 мм, видимые 2 мм (ПВХ/АБС).
4. Присадка по 32-й системе — выполняет цех.
5. Зазор до потолка 100 мм — закрыть планкой в цвет корпуса при монтаже.
6. Навесной корпус — на стене: крепление к стене, 4 точки; основание стены и шаг анкеров — монтажная схема шкафов.

3D орто

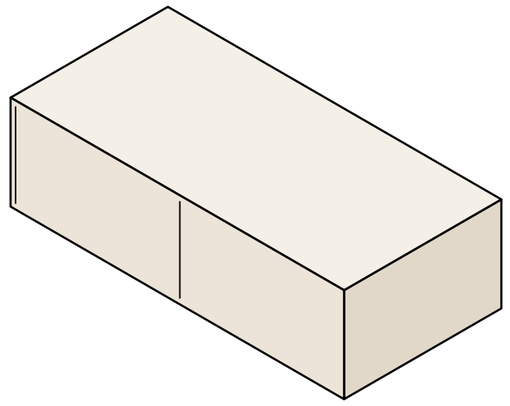


					Проект: Четырёхкомнатная квартира		**М 1:20**
	Лист	№ док.	Подпись	Дата			
Дизайнер	Кырлан А.С.			04.11.26	Система хранения М_32	Стадия	Лист	Листов
						П	Д_9	120


Вид с фасадами

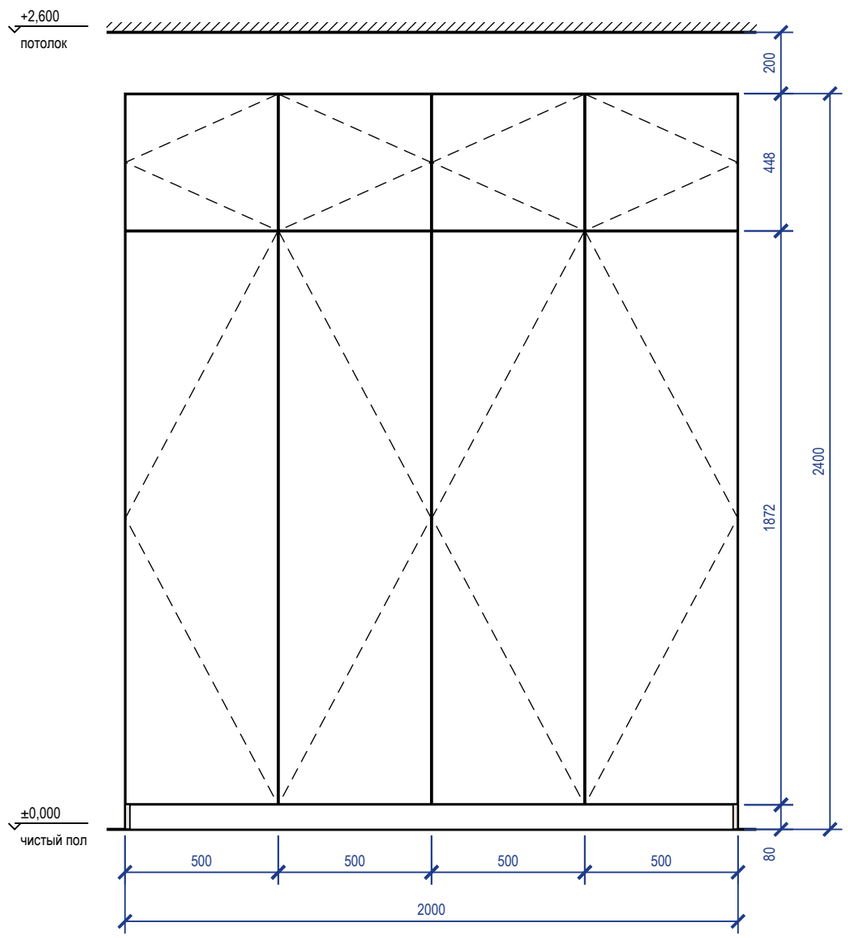


Вид без фасадов

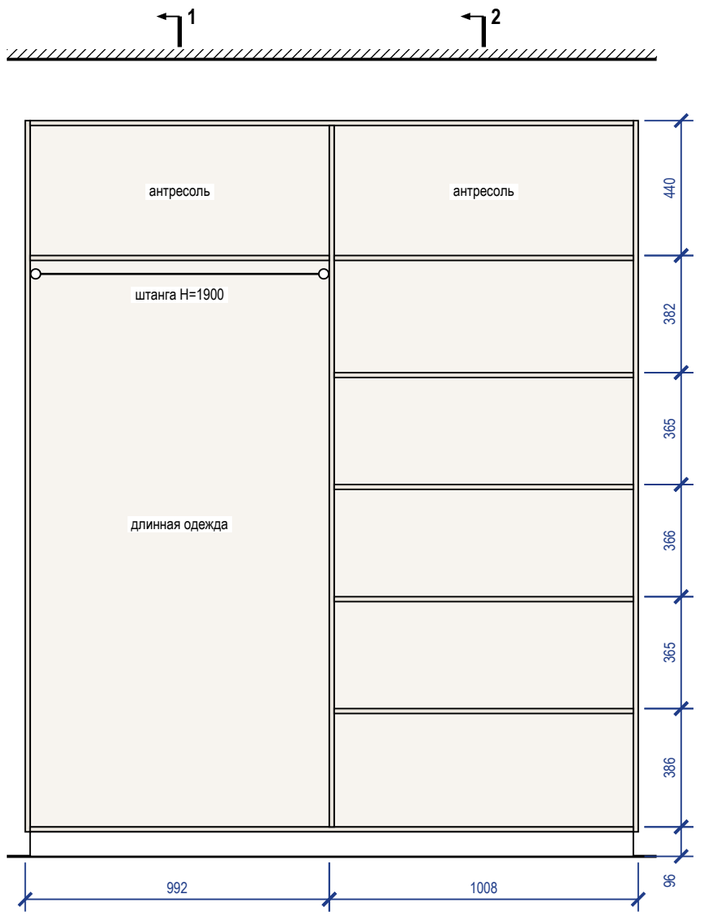

Разрез 1-1

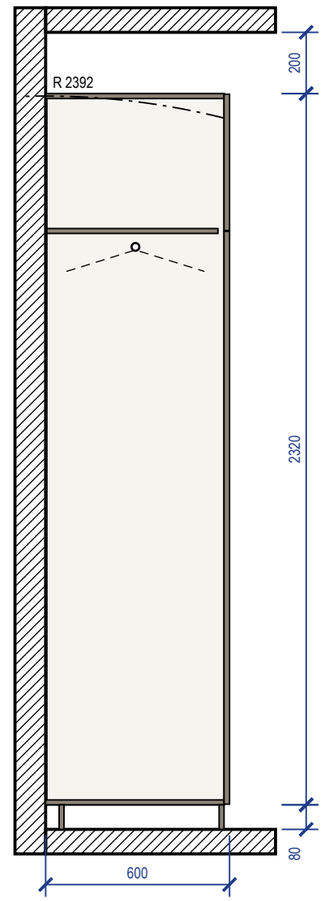


Разрез 2-2

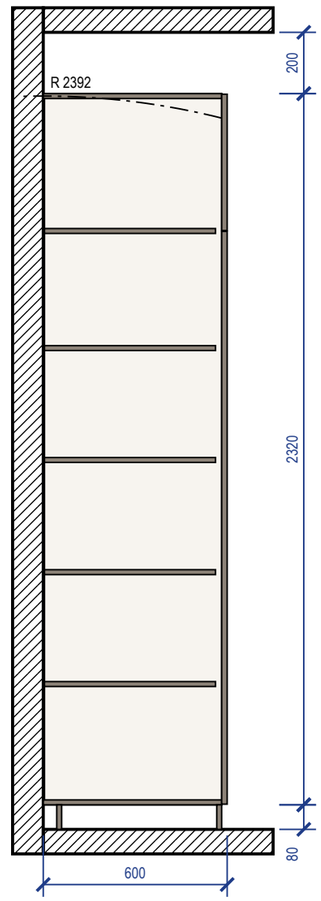

Примечания


1. Размеры — в мм по чистовой отделке; изделие 2000×600×2400 (Ш×Г×В). Перед раскроем — контрольный замер цеха после чистовой отделки стен, пола и потолка.
2. Корпус — ЛДСП 16 мм, задняя стенка ХДФ 4 мм в паз, цоколь 80 мм на регулируемых опорах; фасады накладные — МДФ 18 мм, эмаль матовая, 18 мм; цвет — по колерной карте; петли с доводчиком: фасад 1869 мм — 4 петли, фасад 445 мм — 2 петли.
3. Кромка: скрытые торцы 0,4 мм, видимые 2 мм (ПВХ/АБС).
4. Номинальные зазоры: между фасадами 3 мм, фасад — стена и фасад — потолок не менее 3 мм, фасад ящика — стойка 2 мм.
5. Присадка по 32-й системе — выполняет цех.
6. Зазор до потолка 200 мм.
7. Подъём корпуса: диагональ боковины без цоколя $\sqrt{(2320^2 + 582^2)} = 2392$ мм < 2600 мм до потолка — корпус собирается лёжа, поднимается поворотом и ставится на цоколь.
8. Крепление к стене от опрокидывания: уголок к стене, 3 шт.; основание стены и шаг анкеров — монтажная схема шкафов.

3D орто

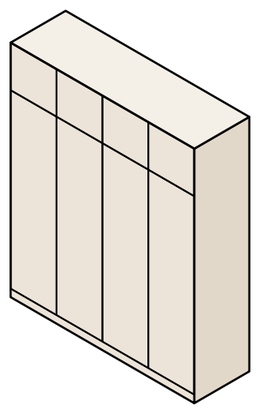


					Проект: Четырёхкомнатная квартира	**М 1:20**
	Лист	№ док.	Подпись	Дата		
Дизайнер	Кырлан А.С.			04.11.26	Шкаф распашной М_34	Стадия: П; Лист: Д_10; Листов: 120


Общий вид

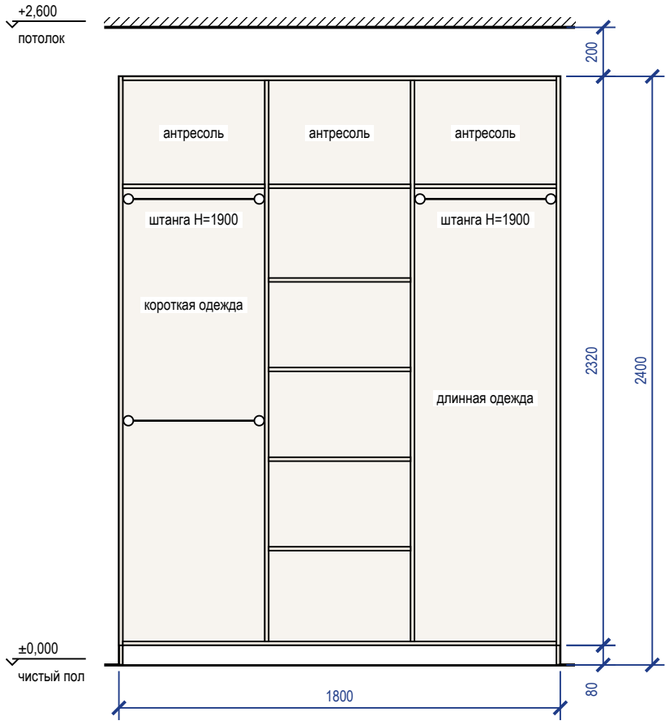


Наполнение, размеры в свету

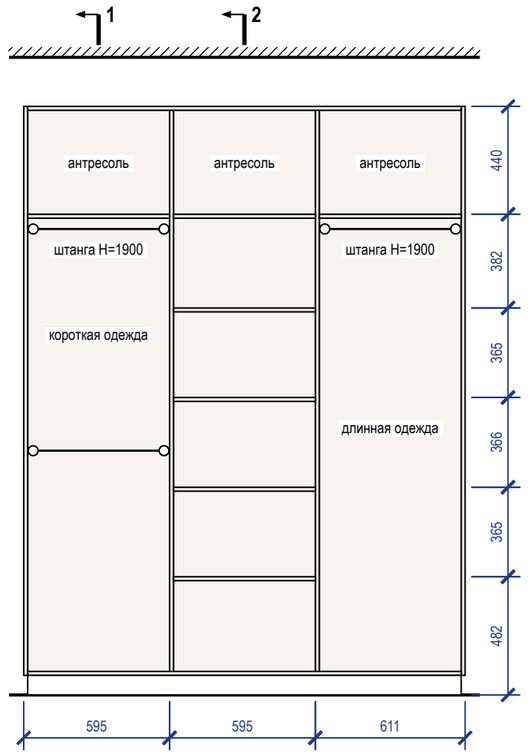

Разрез 1-1

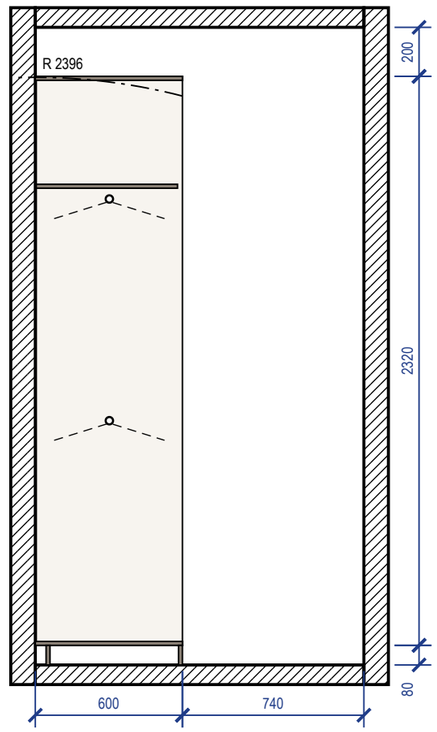


Разрез 2-2

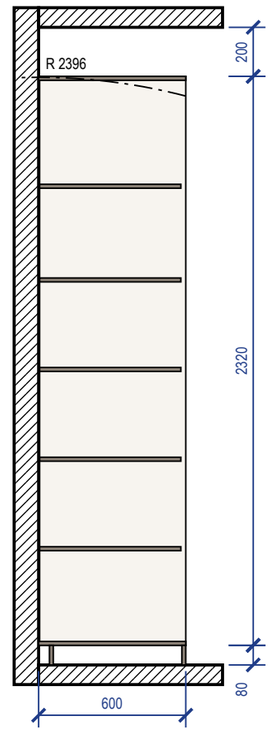

Примечания


1. Размеры — в мм по чистовой отделке; изделие 1800×600×2400 (Ш×Г×В). Перед раскроем — контрольный замер цеха после чистовой отделки стен, пола и потолка.
2. Корпус — ЛДСП 16 мм, задняя стенка ХДФ 4 мм в паз, цоколь 80 мм на регулируемых опорах; открытая система: без фасадов.
3. Кромка: скрытые торцы 0,4 мм, видимые 2 мм (ПВХ/АБС).
4. Присадка по 32-й системе — выполняет цех.
5. Зазор до потолка 200 мм.
6. Подъём корпуса: диагональ боковины без цоколя √(2320² + 600²) = 2396 мм < 2600 мм до потолка — корпус собирается лёжа, поднимается поворотом и ставится на цоколь.
7. Крепление к стене от опрокидывания: крепление к стене, 4 точки; основание стены и шаг анкеров — монтажная схема шкафов.
8. Проход перед изделием 740 мм показан на разрезе 1-1.

3D орто

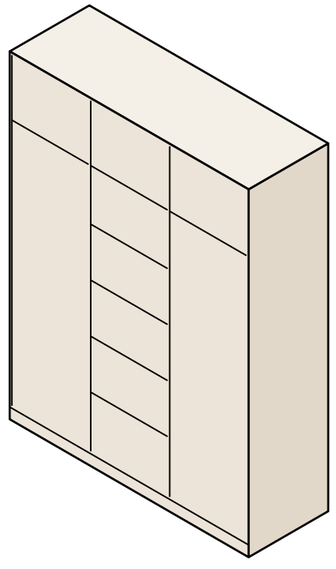


					Проект: Четырёхкомнатная квартира	**М 1:25**
	Лист	№ док.	Подпись	Дата		
Дизайнер	Кырлан А.С.			04.11.26	Система хранения М_38	Стадия: П; Лист: Д_11; Листов: 120


Общий вид

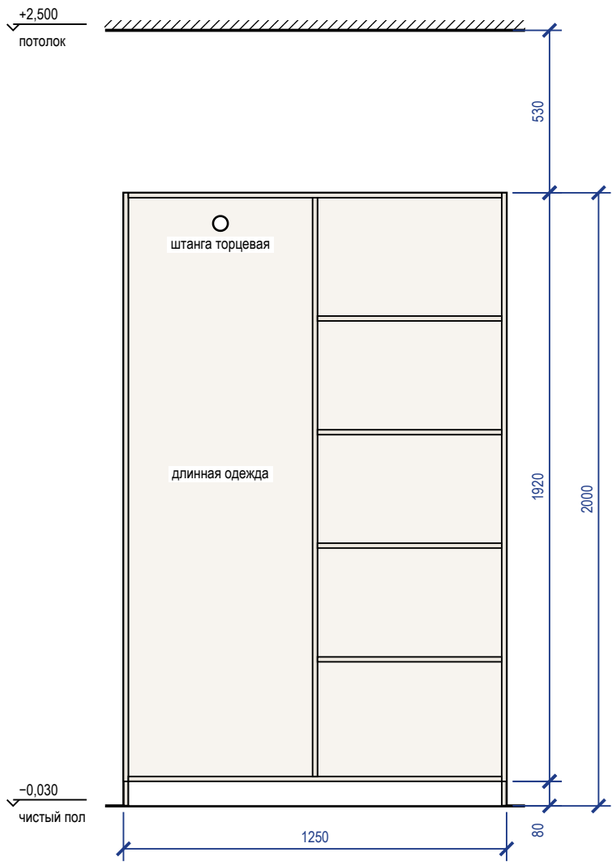


Наполнение, размеры в свету

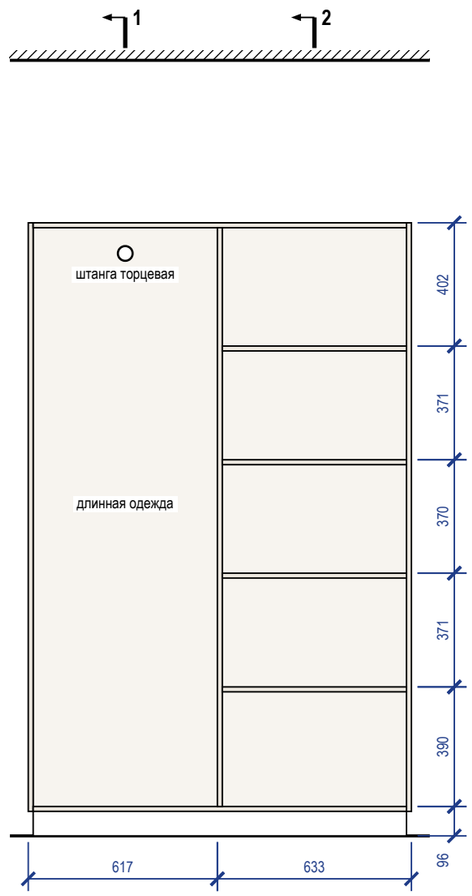

Разрез 1-1

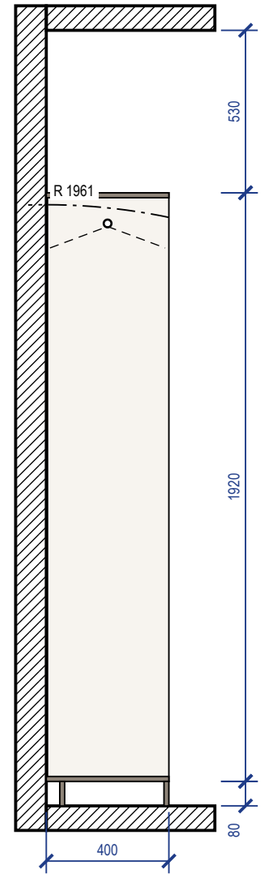


Разрез 2-2

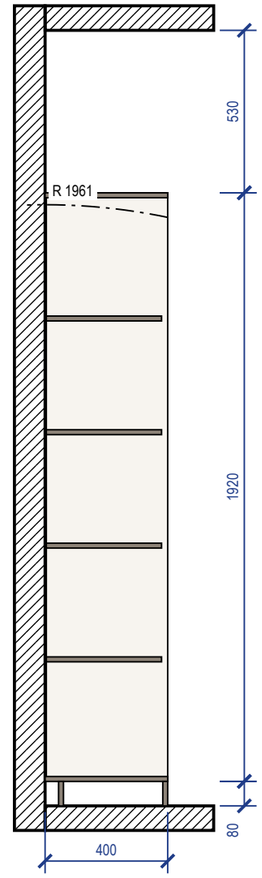

Примечания


1. Размеры — в мм по чистовой отделке; изделие 1250×400×2000 (Ш×Г×В). Перед раскроем — контрольный замер цеха после чистовой отделки стен, пола и потолка.
2. Корпус — ЛДСП 16 мм, задняя стенка ХДФ 4 мм в паз, цоколь 80 мм на регулируемых опорах; открытая система: без фасадов.
3. Кромка: скрытые торцы 0,4 мм, видимые 2 мм (ПВХ/АБС).
4. Присадка по 32-й системе — выполняет цех.
5. Зазор до потолка 530 мм.
6. Подъём корпуса: диагональ боковины без цоколя $\sqrt{(1920^2 + 400^2)} = 1961$ мм < 2530 мм до потолка — корпус собирается лёжа, поднимается поворотом и ставится на цоколь.
7. Крепление к стене от опрокидывания: крепление к стене, 3 точки; основание стены и шаг анкеров — монтажная схема шкафов.

3D орто

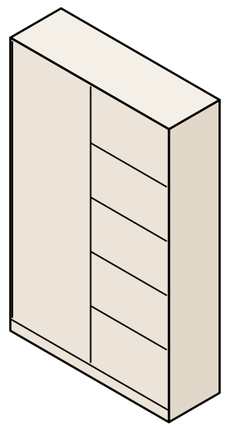


					Проект: Четырёхкомнатная квартира	**М 1:20**
	Лист	№ док.	Подпись	Дата		
Дизайнер	Кырлан А.С.			04.11.26	Система хранения М_39	Стадия: П; Лист: Д_12; Листов: 120


Общий вид

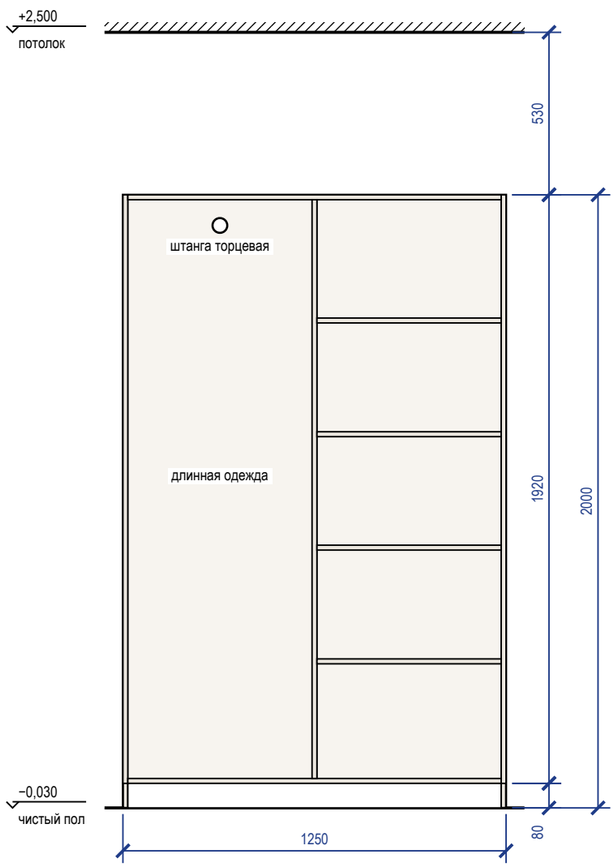


Наполнение, размеры в свету

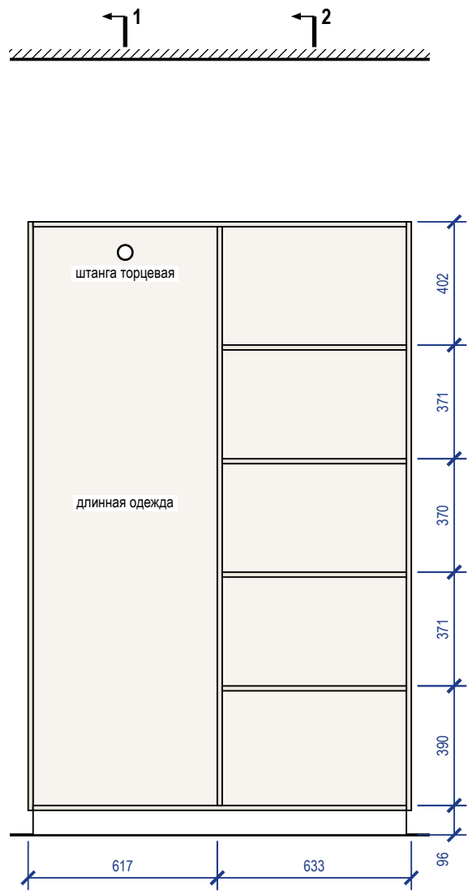

Разрез 1-1

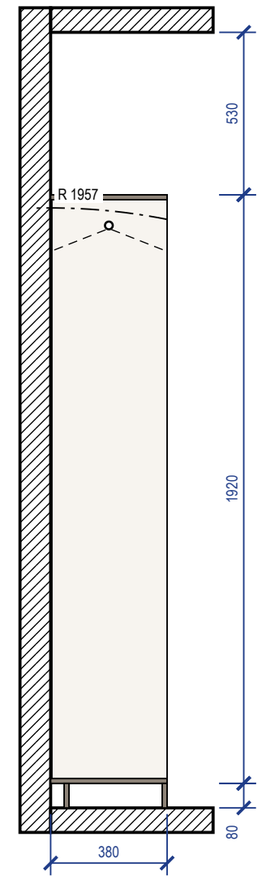


Разрез 2-2

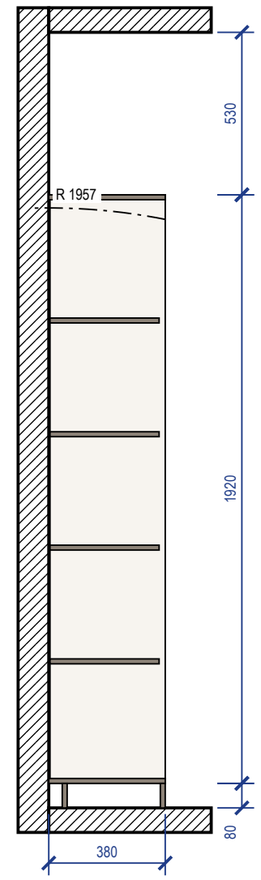

Примечания


1. Размеры — в мм по чистовой отделке; изделие 1250×380×2000 (Ш×Г×В). Перед раскроем — контрольный замер цеха после чистовой отделки стен, пола и потолка.
2. Корпус — ЛДСП 16 мм, задняя стенка ХДФ 4 мм в паз, цоколь 80 мм на регулируемых опорах; открытая система: без фасадов.
3. Кромка: скрытые торцы 0,4 мм, видимые 2 мм (ПВХ/АБС).
4. Присадка по 32-й системе — выполняет цех.
5. Зазор до потолка 530 мм.
6. Подъём корпуса: диагональ боковины без цоколя $\sqrt{(1920^2 + 380^2)} = 1957$ мм < 2530 мм до потолка — корпус собирается лёжа, поднимается поворотом и ставится на цоколь.
7. Крепление к стене от опрокидывания: крепление к стене, 3 точки; основание стены и шаг анкеров — монтажная схема шкафов.

3D орто

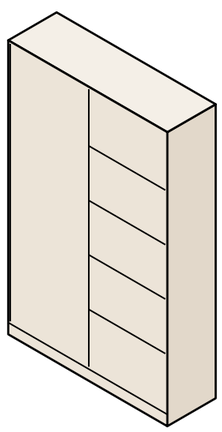


					Проект: Четырёхкомнатная квартира	**М 1:20**
	Лист	№ док.	Подпись	Дата		
Дизайнер	Кырлан А.С.			04.11.26	Система хранения М_40	Стадия: П; Лист: Д_13; Листов: 120


Вид с фасадами

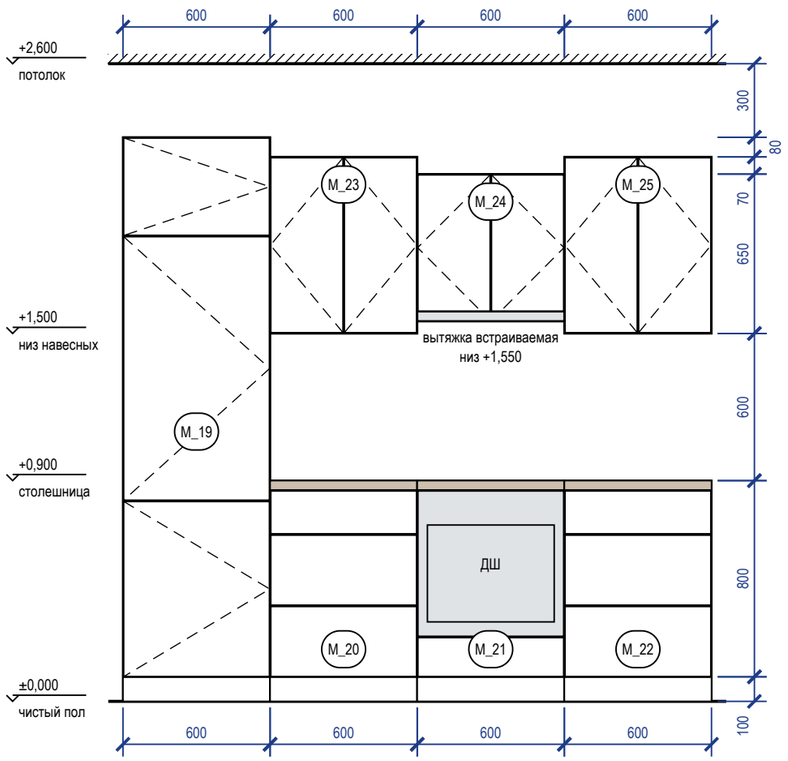


Вид без фасадов (наполнение, выводы)

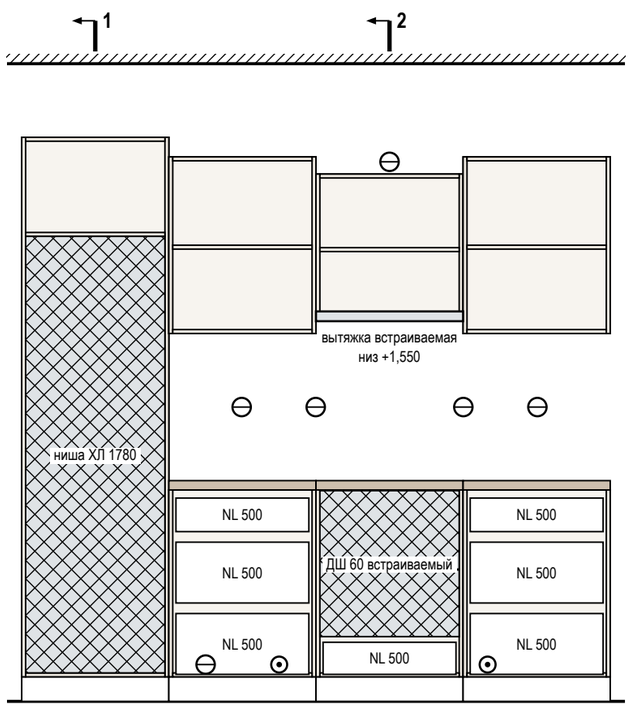


Разрез 1-1

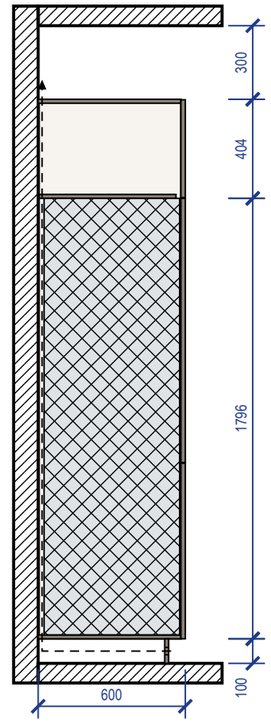

Разрез 2-2

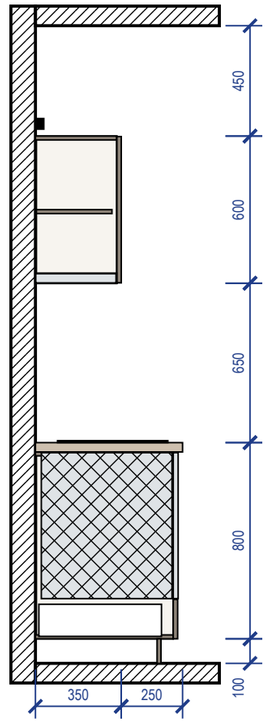

3D орто

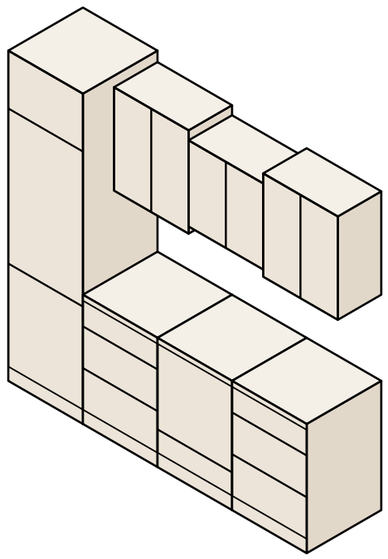


Примечания


1. Размеры — в мм по чистовой отделке, вид из помещения; марки — как на плане расстановки. Перед раскроем — контрольный замер цеха после фартука и пола.
2. Корпуса — ЛДСП 16 мм, задняя стенка ХДФ 4 мм; фасады — МДФ, эмаль матовая 18 мм, цвет по колерной карте; столешница 38 мм, свес 20 мм; цоколь 100 мм.
3. Кромка: скрытые торцы 0,4 мм, видимые 2 мм. Номинальные зазоры: между фасадами 3 мм, фасад — столешница 3 мм, фасад — стена не менее 3 мм.
4. Ящики полного выдвижения и петли — с доводчиком; присадка по 32-й системе — выполняет цех.
5. Вытяжка встраивается в дно навесного модуля M_24 над варочной: её низ на 1550 мм от пола, 650 мм над панелью (не меньше 650 мм).
6. Ниши техники (холодильник — ориентир 1780 мм) — по монтажным схемам выбранных моделей: решётка в цоколе и канал за пеналом холодильника, зазор за духовым шкафом, фасад ПММ на двери машины.

					Проект: Четырёхкомнатная квартира	**М 1:25**
	Лист	№ док.	Подпись	Дата	Кухня (пом. 6). Развёртка гарнитура	Стадия / Лист / Листов
Дизайнер	Кырлан А.С.			04.11.26		П / Д_14 / 120


Вид с фасадами

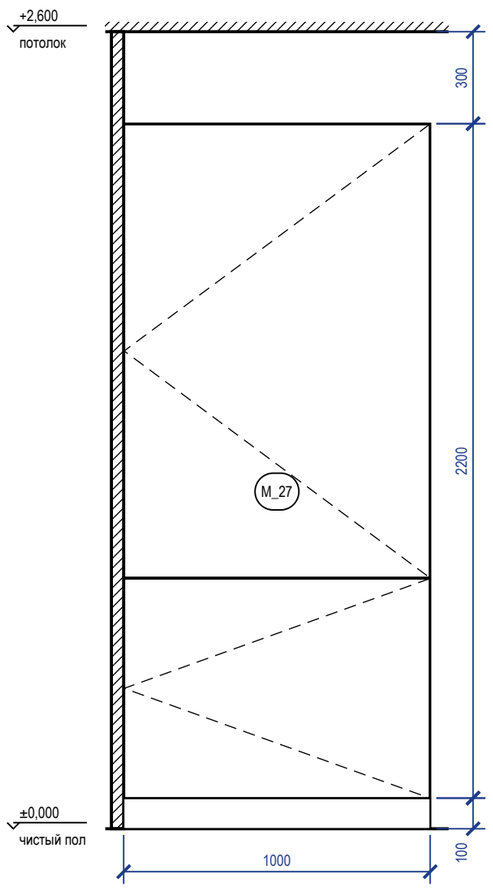


Вид без фасадов (наполнение, выводы)

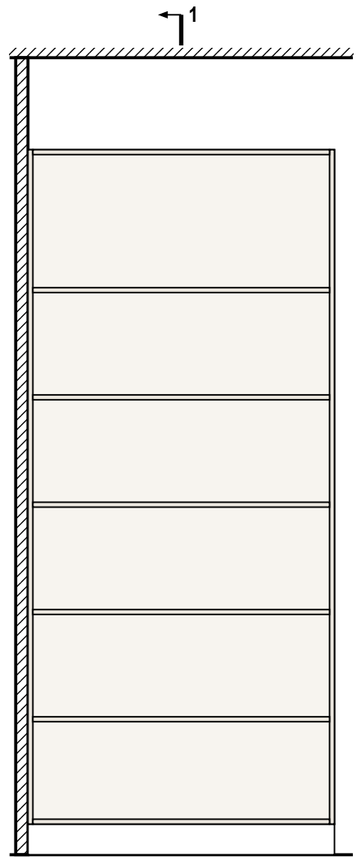

Разрез 1-1

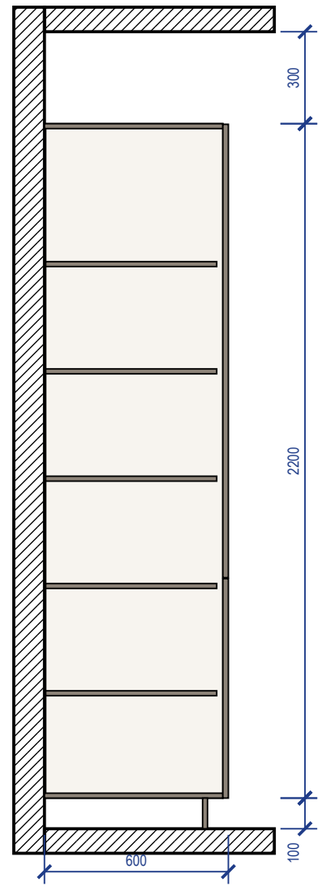

3D орто

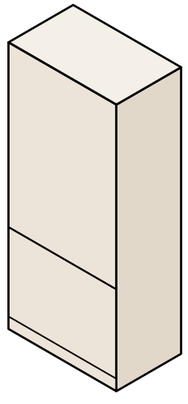


Примечания

1. Размеры — в мм по чистовой отделке, вид из помещения; марки — как на плане расстановки. Перед раскроем — контрольный замер цеха после фартука и пола.
2. Корпуса — ЛДСП 16 мм, задняя стенка ХДФ 4 мм; фасады — МДФ, эмаль матовая 18 мм, цвет по колерной карте; столешница 38 мм, свес 20 мм; цоколь 100 мм.
3. Кромка: скрытые торцы 0,4 мм, видимые 2 мм. Номинальные зазоры: между фасадами 3 мм, фасад — столешница 3 мм, фасад — стена не менее 3 мм.
4. Ящики полного выдвижения и петли — с доводчиком; присадка по 32-й системе — выполняет цех.
5. Ниши техники — по монтажным схемам выбранных моделей: решётка в цоколе и канал за пеналом холодильника, зазор за духовым шкафом, фасад ПММ на двери машины.


					Проект: Четырёхкомнатная квартира	**М 1:20**
	Лист	№ док.	Подпись	Дата	Кухня (пом. 6). Развёртка гарнитура	Стадия / Лист / Листов
Дизайнер	Кырлан А.С.			04.11.26		П / Д_15 / 120

План (вид сверху)

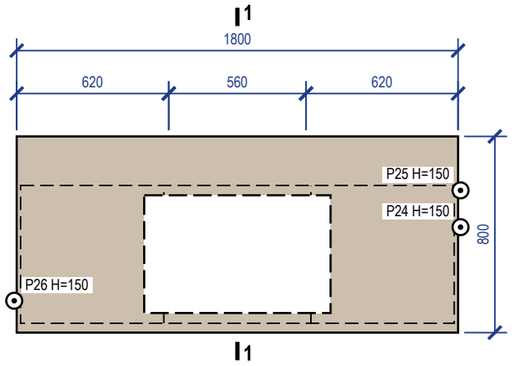


▲ рабочая сторона — северная (к стене А), проход 1200


Вид с рабочей стороны

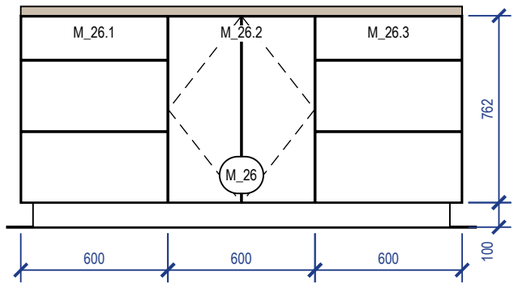


Вид без фасадов (наполнение, вывод)

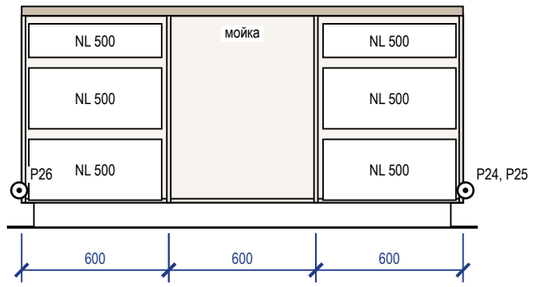

Разрез 1-1

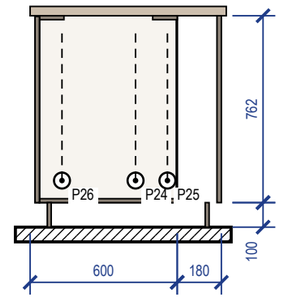

3D орто

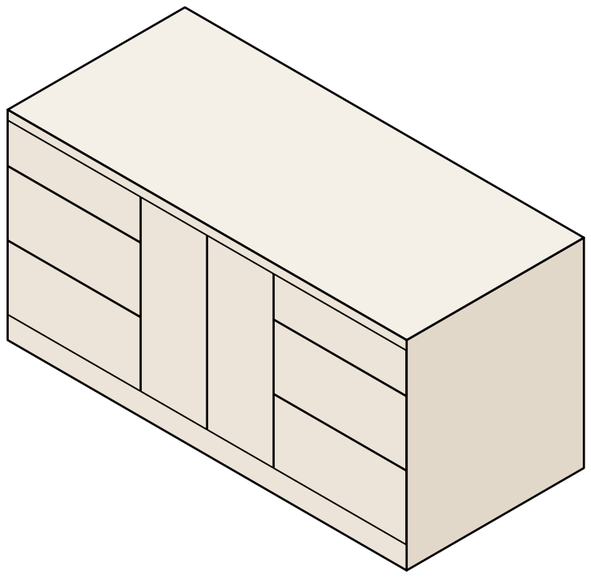

Примечания

1. Размеры — в мм по чистовому полу; перед раскроем — контрольный замер цеха после укладки пола. Остров крепится к полу (уголки в цоколе), выравнивается опорами ±20 мм.
2. Корпуса — ЛДСП 16 мм, задняя стенка ХДФ 4 мм; фасады — МДФ, эмаль матовая 18 мм; столешница 38 мм, свес 20 мм по периметру; цоколь 100 мм с отступом 50 мм.
3. Кромка: скрытые торцы 0,4 мм, видимые 2 мм. Номинальные зазоры: между фасадами 3 мм, фасад — столешница 3 мм.
4. Рабочая сторона — северная (к стене А): проход 1200 мм; с тыла — глухая панель. Членение и сторона — предложение мебельщика.
5. Питание: P24 — торцевая панель острова M_26: мелкая техника, H=150; P25 — торцевая панель острова M_26: мелкая техника, H=150; P26 — посудомоечная машина в острове M_26, H=150; кабель — внутри модуля до панели, доступ через съёмный цоколь.

Спецификация изделия M_26

Поз.	Наименование	Тип, размер	Кол.
M_26.1	модуль с ящиками	600×800×900	1
M_26.2	модуль под мойку	600×800×900	1
M_26.3	модуль с ящиками	600×800×900	1
M_26.2	Мойка врезная / подстольная с сифоном	вырез по шаблону, ориентир 760 × 480	1
	Направляющие полного выдвижения с доводчиком NL 500	пара	6
	Ручка-профиль	латунь матовая	8
	Петля накладная 110° с доводчиком	чашка 35 мм	4
	Опора кухонная регулируемая 100–120 мм	+ клипса цоколя	12
	Уголок крепления острова к полу	стальной, в цоколе	4

	Лист	№ док.	Подпись	Дата
Дизайнер	Кырлан А.С.			04.11.26

Проект: Четырёхкомнатная квартира — **M 1:25**

Остров M_26 (пом. 6). Чертёж изделия

Стадия	Лист	Листов
П	Д_16	120

Ведомость отделки помещений (форма 1 прил. А ГОСТ 21.501-2018). Лист 1 из 3

№	Наименование помещения	Потолок			Стены и перегородки			Низ стен (плинтус)			Пол		Примечание
		Вид отделки	Код цвета	S, м²	Вид отделки	Код цвета	S, м²	Вид отделки	Код цвета	L, м	Вид отделки	S, м²	
1	Зал 18,16 м²	ГКЛ по каркасу П113, отм. +2,500; +2,600; окраска, Tikkurila Anti-Reflex 2, глубокоматовая, 2 слоя, подготовка Q3	Tikkurila F497	18,16	Окраска, Tikkurila Optiva 5 Matt, матовая, 2 слоя, подготовка К3 Акцент — стена А: окраска, Tikkurila Optiva 5 Matt, матовая, 3 слоя, аналог: интерьерная краска, класс 2 по EN 13300, глубокоматовая/матовая, база С, подготовка К3	Tikkurila F497 Tikkurila L481	25,94 13,55	Плинтус МДФ h=80 мм, аналог: МДФ под окраску 80×16 мм	Tikkurila F497	16,6	Инженерная доска, аналог: дуб натуральный брашированный, масло-воск, 14/4 мм, на клею; тип 1, отм. ЧП ±0,000	18,16	Н стен 2500 (до потолка); колеруется в код стен, но по эмали на МДФ: сличать отдельным выкрасом на своей подложке (выкрас № 10); плинтус в цвет: стены
2	Ванная комната 5,57 м²	ГКЛВ по каркасу П113, отм. +2,500; окраска, Tikkurila Luja 7, матовая, 2 слоя, подготовка Q3	Tikkurila F497	5,57	Облицовка плиткой, аналог: керамогранит матовый, тон F497, 600×600×9 мм, клей С2 TE S1, затирка CG2WA	#F1F1EC	22,35	нет (облицовка от пола)			Аналог: керамогранит матовый R10, тон J484, 600×600×10 мм; тип 2, отм. ЧП −0,015	5,57	Н стен 2515 (до потолка); тёплый пол; гидроизоляция обмазочная, 2 слоя, по всему помещению, с заведением на стены 200 мм; над ванной — до 2100 и 300 мм за борт (по пирогу пола); тест проливом и акт скрытых работ; облицовка от чистого пола до низа потолка; по ГКЛВ каркаса П113, влагостойкая окраска; Q3
3	Тёмная комната 2,96 м²	ГКЛ по каркасу П113, отм. +2,600; окраска, Tikkurila Anti-Reflex 2, глубокоматовая, 2 слоя, подготовка Q3	Tikkurila F497	2,96	Окраска, Tikkurila Optiva 5 Matt, матовая, 2 слоя, подготовка К3	Tikkurila F497	16,94	Плинтус МДФ h=80 мм, аналог: МДФ под окраску 80×16 мм	Tikkurila F497	6,4	Инженерная доска, аналог: дуб натуральный брашированный, масло-воск, 14/4 мм, на клею; тип 1, отм. ЧП ±0,000	2,96	Н стен 2600 (до потолка); колеруется в код стен, но по эмали на МДФ: сличать отдельным выкрасом на своей подложке (выкрас № 10); плинтус в цвет: стены
4	Детская 1 17,51 м²	ГКЛ по каркасу П113, отм. +2,600; окраска, Tikkurila Anti-Reflex 2, глубокоматовая, 2 слоя, подготовка Q3	Tikkurila F497	17,51	Окраска, Tikkurila Joker, полуматовая, 2 слоя, подготовка К3	Tikkurila F497	40,12	Плинтус МДФ h=80 мм, аналог: МДФ под окраску 80×16 мм	Tikkurila F497	16,2	Инженерная доска, аналог: дуб натуральный брашированный, масло-воск, 14/4 мм, на клею; тип 1, отм. ЧП ±0,000	17,51	Н стен 2600 (до потолка); колеруется в код стен, но по эмали на МДФ: сличать отдельным выкрасом на своей подложке (выкрас № 10); плинтус в цвет: стены
5	Коридор 4,54 м²	ГКЛ по каркасу П113, отм. +2,600; окраска, Tikkurila Anti-Reflex 2, глубокоматовая, 2 слоя, подготовка Q3	Tikkurila F497	4,54	Окраска, Tikkurila Optiva 20 Semimatt, полуматовая, 2 слоя, подготовка К3	Tikkurila J484	22,21	Плинтус МДФ h=80 мм, аналог: МДФ под окраску 80×16 мм	Tikkurila J484	8,1	Аналог: керамогранит матовый R10, тон V486, 600×600×10 мм; тип 3, отм. ЧП ±0,000	4,54	Н стен 2600 (до потолка); колеруется в код стен, но по эмали на МДФ: сличать отдельным выкрасом на своей подложке (выкрас № 10); плинтус в цвет: стены
6	Кухня 15,19 м²	ГКЛ по каркасу П113, отм. +2,600; окраска, Tikkurila Luja 7, матовая, 2 слоя, подготовка Q3	Tikkurila F497	15,19	Окраска, Tikkurila Luja 7, полуматовая, 2 слоя, подготовка К3 Фартук кухни (стена А): облицовка керамогранитом, аналог: керамогранит матовый, тон F497, 600×600×9 мм, клей С2 TE S1, затирка CG2WA	Tikkurila F497 #F1F1EC	34,48 1,11	Плинтус МДФ h=80 мм, аналог: МДФ под окраску 80×16 мм	Tikkurila F497	13,8	Инженерная доска, аналог: дуб натуральный брашированный, масло-воск, 14/4 мм, на клею; тип 4, отм. ЧП ±0,000	15,19	Н стен 2600 (до потолка); гидроизоляция обмазочная, 2 слоя, с заведением на стены 200 мм (по пирогу пола); тест проливом и акт скрытых работ; влагостойкая полуматовая окраска (класс мокрого истирания 1 по EN 13300); категория К3 по СП 71.13330.2017, табл. 7.5; по ГКЛ каркаса П113, влагостойкая окраска; Q3 колеруется в код стен, но по эмали на МДФ: сличать отдельным выкрасом на своей подложке (выкрас № 10); плинтус в цвет: стены

Примечания

1. Ведомость продолжена на листе 2 из 3; итоги, сводка площадей и примечания — на последнем листе ведомости.

					Проект: Четырёхкомнатная квартира
	Лист	№ док.	Подпись	Дата	
Дизайнер	Кырлан А.С.			04.11.26	Ведомость отделки помещений. Лист 1 из 3

Стадия	Лист	Листов
П	С1	120

Ведомость отделки помещений (форма 1 прил. А ГОСТ 21.501-2018). Лист 2 из 3

№	Наименование помещения	Потолок			Стены и перегородки			Низ стен (плинтус)			Пол		Примечание
		Вид отделки	Код цвета	S, м²	Вид отделки	Код цвета	S, м²	Вид отделки	Код цвета	L, м	Вид отделки	S, м²	
7	Прихожая-коридор 7,80 м²	ГКЛ по каркасу П113, отм. +2,600; окраска, Tikkurila Anti-Reflex 2, глубокоматовая, 2 слоя, подготовка Q3	Tikkurila F497	7,80	Окраска, Tikkurila Optiva 20 Semimatt, полуматовая, 2 слоя, подготовка К3	Tikkurila J484	23,80	Плинтус МДФ h=80 мм, аналог: МДФ под окраску 80×16 мм	Tikkurila J484	8,7	Аналог: керамогранит матовый R10, тон V486, 600×600×10 мм; тип 3, отм. ЧП ±0,000	7,80	Н стен 2600 (до потолка); колеруется в код стен, но по эмали на МДФ: сличать отдельным выкрасом на своей подложке (выкрас № 10); плинтус в цвет: стены
8	Гардеробная 2 1,29 м²	ГКЛ по каркасу П113, отм. +2,600; окраска, Tikkurila Anti-Reflex 2, глубокоматовая, 2 слоя, подготовка Q3	Tikkurila F497	1,29	Окраска, Tikkurila Optiva 5 Matt, матовая, 2 слоя, подготовка К3	Tikkurila F497	8,65	Плинтус МДФ h=80 мм, аналог: МДФ под окраску 80×16 мм	Tikkurila F497	3,3	Инженерная доска, аналог: дуб натуральный брашированный, масло-воск, 14/4 мм, на клею; тип 1, отм. ЧП ±0,000	1,29	Н стен 2600 (до потолка); колеруется в код стен, но по эмали на МДФ: сличать отдельным выкрасом на своей подложке (выкрас № 10); плинтус в цвет: стены
9	Детская 2 10,96 м²	ГКЛ по каркасу П113, отм. +2,600; окраска, Tikkurila Anti-Reflex 2, глубокоматовая, 2 слоя, подготовка Q3	Tikkurila F497	10,96	Окраска, Tikkurila Joker, полуматовая, 2 слоя, подготовка К3	Tikkurila F497	29,08	Плинтус МДФ h=80 мм, аналог: МДФ под окраску 80×16 мм	Tikkurila F497	11,8	Инженерная доска, аналог: дуб натуральный брашированный, масло-воск, 14/4 мм, на клею; тип 1, отм. ЧП ±0,000	10,96	Н стен 2600 (до потолка); колеруется в код стен, но по эмали на МДФ: сличать отдельным выкрасом на своей подложке (выкрас № 10); плинтус в цвет: стены
10	Санузел 1,31 м²	ГКЛВ по каркасу П113, отм. +2,500; окраска, Tikkurila Luja 7, матовая, 2 слоя, подготовка Q3	Tikkurila F497	1,31	Облицовка плиткой, аналог: керамогранит матовый, тон F497, 600×600×9 мм, клей C2 TE S1, затирка CG2WA	#F1F1EC	10,46	нет (облицовка от пола)			Аналог: керамогранит матовый R10, тон J484, 600×600×10 мм; тип 2, отм. ЧП −0,015	1,31	Н стен 2515 (до потолка); тёплый пол; гидроизоляция обмазочная, 2 слоя, по всему помещению, с заведением на стены 200 мм (по пирогу пола); тест проливом и акт скрытых работ; облицовка от чистого пола до низа потолка; по ГКЛВ каркаса П113, влагостойкая окраска; Q3
11	Гостиная 14,55 м²	ГКЛ по каркасу П113, отм. +2,600; окраска, Tikkurila Anti-Reflex 2, глубокоматовая, 2 слоя, подготовка Q3	Tikkurila F497	14,55	Окраска, Tikkurila Optiva 5 Matt, матовая, 2 слоя, подготовка К3 Акцент — стена А: окраска, Tikkurila Optiva 5 Matt, матовая, 3 слоя, аналог: интерьерная краска, класс 2 по EN 13300, глубокоматовая/матовая, база С, подготовка К3	Tikkurila F497 Tikkurila L481	27,79 11,13	Плинтус МДФ h=80 мм, аналог: МДФ под окраску 80×16 мм	Tikkurila F497	15,6	Инженерная доска, аналог: дуб натуральный брашированный, масло-воск, 14/4 мм, на клею; тип 1, отм. ЧП ±0,000	14,55	Н стен 2600 (до потолка); колеруется в код стен, но по эмали на МДФ: сличать отдельным выкрасом на своей подложке (выкрас № 10); плинтус в цвет: стены
12	Гардеробная 1 2,83 м²	ГКЛ по каркасу П113, отм. +2,600; окраска, Tikkurila Anti-Reflex 2, глубокоматовая, 2 слоя, подготовка Q3	Tikkurila F497	2,83	Окраска, Tikkurila Optiva 5 Matt, матовая, 2 слоя, подготовка К3	Tikkurila F497	14,96	Плинтус МДФ h=80 мм, аналог: МДФ под окраску 80×16 мм	Tikkurila F497	5,5	Инженерная доска, аналог: дуб натуральный брашированный, масло-воск, 14/4 мм, на клею; тип 1, отм. ЧП ±0,000	2,83	Н стен 2600 (до потолка); колеруется в код стен, но по эмали на МДФ: сличать отдельным выкрасом на своей подложке (выкрас № 10); плинтус в цвет: стены
13	Балкон 1 3,70 м²	ГКЛВ по каркасу П113, отм. +2,500; окраска, Tikkurila Luja 7, матовая, 2 слоя, подготовка Q3	Tikkurila F497	3,70	Окраска, Tikkurila Luja 7, полуматовая, 2 слоя, подготовка К3	Tikkurila F497	16,51	Плинтус из керамогранита h=80 мм, аналог: из керамогранита пола, подрезка 80 мм, верхняя кромка с запилом 45°	#B8AFA5	7,7	Аналог: керамогранит матовый R11, тон V486, 600×600×10 мм; тип 5, отм. ЧП −0,030	3,70	Н стен 2530 (до потолка); влагостойкая окраска по утеплённой стене; категория К3 по СП 71.13330.2017, табл. 7.5; по ГКЛВ каркаса П113, влагостойкая окраска; Q3

Примечания

1. Ведомость продолжена на листе 3 из 3; итоги, сводка площадей и примечания — на последнем листе ведомости.

					Проект: Четырёхкомнатная квартира
	Лист	№ док.	Подпись	Дата	Ведомость отделки помещений. Лист 2 из 3
Дизайнер	Кырлан А.С.			04.11.26	

Стадия	Лист	Листов
П	С2	120

Ведомость отделки помещений (форма 1 прил. А ГОСТ 21.501-2018). Лист 3 из 3

№	Наименование помещения	Потолок			Стены и перегородки			Низ стен (плинтус)			Пол		Примечание
		Вид отделки	Код цвета	S, м²	Вид отделки	Код цвета	S, м²	Вид отделки	Код цвета	L, м	Вид отделки	S, м²	
	Итого			**106,37**			**319,07**			**113,7**		**106,37**	

Сводка площадей по материалам отделки

Поверхность	Материал / код цвета	Серия	Площадь, м²
Потолок	Tikkurila F497	Anti-Reflex 2	80,60
Потолок	Tikkurila F497	Luja 7	25,77
Стены	Tikkurila F497	Optiva 5 Matt	94,28
Стены	Tikkurila L481	Optiva 5 Matt	24,68
Стены	облицовка плиткой 600×600×9 мм, #F1F1EC	аналог: керамогранит матовый, тон F497	32,81
Стены	Tikkurila F497	Joker	69,20
Стены	Tikkurila J484	Optiva 20 Semimatt	46,01
Стены	Tikkurila F497	Luja 7	50,99
Фартук	облицовка керамогранитом 600×600×9 мм, #F1F1EC	аналог: керамогранит матовый, тон F497	1,11

Примечания

1. Площади поверхностей — по чистым граням стен до отделки: стены = периметр × высоту от чистого пола помещения до низа потолка минус проёмы (облицовка плиткой — до верха облицовки); плинтус = периметр минус дверные проёмы; пол и потолок — по площади помещения. Количество плиток по раскладке. Площади помещений — с учётом всех частей помещения; откосы в площадь стен не входят.
2. Акцентные стены и фартук — отдельными строками, их площадь вычтена из основной отделки стен помещения; фартук — над нижними модулями кухни от столешницы до низа навесных шкафов, где шкафов нет — на 600 мм.
3. Плинтус — длина по периметру за вычетом дверных проёмов; примыкания к наличникам и встроенной мебели — по развёрткам.
4. Формат плитки — Ш×В×Т (ширина × высота в положении укладки × толщина), мм; на полу — вдоль стен А/В × вдоль стен Б/Г.
5. Коды цвета — по веерам производителей; колеровка каждой краски одной партией, проверка выкраса при свете D65 и при лампах проекта.
6. Уровни подготовки Q1–Q4 — система Knauf, не норма ГОСТ/СП; допуски поверхностей — по СП 71.13330.2017 (действующая редакция).
7. «аналог:» — изделие задано характеристиками, марку и артикул согласовать с заказчиком до закупки.
8. Плавающая стяжка по звукоизоляции: демпферная (кромочная) лента по контуру помещения и у стояков (СП 51.13330.2011, п. 9.11); плинтус крепится только к стене.

					Проект: Четырёхкомнатная квартира
	Лист	№ док.	Подпись	Дата	Ведомость отделки помещений. Лист 3 из 3
Дизайнер	Кырлан А.С.			04.11.26	

Стадия	Лист	Листов
П	С3	120

Поз.	Наименование и техническая характеристика	Тип, марка, обозначение документа	Код продукции	Поставщик	Ед. изм.	Кол.	Образец	Примечание
	Лакокрасочные материалы							
1	Краска интерьерная водно-дисперсионная акриловая для стен, матовая, класс мокрого истирания 2 по EN 13300, база A; цвет по вееру Tikkurila F497 «Paper», колеровка машинная	Tikkurila Optiva 5 Matt		Tikkurila	л	26,1		поз. К1 колерной карты; пом. 1, 3, 8, 11, 12; S = 94,3 м² × 2 сл. × 0,12 л/м² = 22,6 л, +10 % и 0,5 л на подкраску → ≥ 25,4 л; тара 2 × 9 л + 3 × 2,7 л
2	Краска интерьерная водно-дисперсионная акриловая для акцентных стен, матовая, класс мокрого истирания 2 по EN 13300, база C; цвет по вееру Tikkurila L481 «Silhouette», колеровка машинная	Tikkurila Optiva 5 Matt		Tikkurila	л	10,8		поз. К2 колерной карты; пом. 1, 11; S = 24,7 м² × 3 сл. × 0,12 л/м² = 8,9 л, +10 % и 0,5 л на подкраску → ≥ 10,3 л; тара 1 × 9 л + 2 × 0,9 л
3	Краска интерьерная водно-дисперсионная акриловая для потолков, глубокоматовая, класс мокрого истирания 2 по EN 13300, база A; цвет по вееру Tikkurila F497 «Paper», колеровка машинная	Tikkurila Anti-Reflex 2		Tikkurila	л	22,5		поз. К3 колерной карты; пом. 1, 3, 4, 5, 7, 8, 9, 11, 12; S = 80,6 м² × 2 сл. × 0,12 л/м² = 19,3 л, +10 % и 0,5 л на подкраску → ≥ 21,8 л; тара 2 × 9 л + 1 × 2,7 л + 2 × 0,9 л
4	Краска интерьерная водно-дисперсионная акриловая для потолков, матовая, класс мокрого истирания 1 по EN 13300, база A; цвет по вееру Tikkurila F497 «Paper», колеровка машинная	Tikkurila Luja 7		Tikkurila	л	8,1		поз. К5 колерной карты; пом. 2, 6, 10, 13; S = 25,8 м² × 2 сл. × 0,12 л/м² = 6,2 л, +10 % и 0,5 л на подкраску → ≥ 7,3 л; тара 3 × 2,7 л
5	Краска интерьерная водно-дисперсионная акриловая для стен, полуматовая, класс мокрого истирания 2 по EN 13300, база A; цвет по вееру Tikkurila F497 «Paper», колеровка машинная	Tikkurila Joker		Tikkurila	л	18,9		поз. К6 колерной карты; пом. 4, 9; S = 69,2 м² × 2 сл. × 0,12 л/м² = 16,6 л, +10 % и 0,5 л на подкраску → ≥ 18,8 л; тара 2 × 9 л + 1 × 0,9 л
6	Краска интерьерная водно-дисперсионная акриловая для стен, полуматовая, класс мокрого истирания 2 по EN 13300, база A; цвет по вееру Tikkurila J484 «Castle», колеровка машинная	Tikkurila Optiva 20 Semimatt		Tikkurila	л	13,5		поз. К7 колерной карты; пом. 5, 7; S = 46,0 м² × 2 сл. × 0,12 л/м² = 11,0 л, +10 % и 0,5 л на подкраску → ≥ 12,6 л; тара 1 × 9 л + 1 × 2,7 л + 2 × 0,9 л
7	Краска интерьерная водно-дисперсионная акриловая для стен, полуматовая, класс мокрого истирания 1 по EN 13300, база A; цвет по вееру Tikkurila F497 «Paper», колеровка машинная	Tikkurila Luja 7		Tikkurila	л	14,4		поз. К9 колерной карты; пом. 6, 13; S = 51,0 м² × 2 сл. × 0,12 л/м² = 12,2 л, +10 % и 0,5 л на подкраску → ≥ 14,0 л; тара 1 × 9 л + 2 × 2,7 л
8	Акрилово-уретановая эмаль на водной основе, полуглянцевая в цвет Tikkurila F497 «Paper» — окраска плинтуса	аналог по характеристикам			л	2,3		поз. К4; пом. 1, 3, 4, 6, 8, 9, 11, 12; L = 89,2 м, S = 8,6 м² × 2 сл. × 0,12 л/м² + 10 %; продукт подобрать в веере Tikkurila
9	Акрилово-уретановая эмаль на водной основе, полуглянцевая в цвет Tikkurila J484 «Castle» — окраска плинтуса	аналог по характеристикам			л	0,5		поз. К8; пом. 5, 7; L = 16,8 м, S = 1,6 м² × 2 сл. × 0,12 л/м² + 10 %; продукт подобрать в веере Tikkurila
10	Грунтовка акриловая под окраску стен и потолков — из системы производителя краски	по системе краски			м²	392		площадь окраски стен, акцентов и потолков; 1 слой перед окраской; расход — по ТУ грунтовки

					Проект: Четырёхкомнатная квартира
	Лист	№ док.	Подпись	Дата	Спецификация отделочных материалов
Дизайнер	Кырлан А.С.			04.11.26	

Стадия	Лист	Листов
П	С4	120

Поз.	Наименование и техническая характеристика	Тип, марка, обозначение документа	Код продукции	Поставщик	Ед. изм.	Кол.	Образец	Примечание
	Плитка и керамогранит							
11	Керамогранит матовый R10, тон J484, 600.8×600.8 мм	аналог по характеристикам			м²	10,47		шов 2 мм; Ванная комната, пол; Санузел, пол; по раскладке 26 шт (S = 6,88 м²), с запасом 29 шт
12	Керамогранит матовый, тон F497, 600.8×600.8 мм	аналог по характеристикам			м²	63,17		шов 2 мм; Ванная комната, стены А–Г; Ванная комната, короб инсталляции; Санузел, стены А–Г; Санузел, короб инсталляции; по раскладке 157 шт (S = 34,22 м²), с запасом 175 шт
13	Керамогранит матовый R10, тон V486, 600.8×600.8 мм	аналог по характеристикам			м²	15,88		шов 2 мм; Коридор, пол; Прихожая-коридор, пол; по раскладке 39 шт (S = 12,34 м²), с запасом 44 шт
14	Керамогранит матовый, тон F497, 600.8×600.8 мм	аналог по характеристикам			м²	1,80		шов 2 мм; Кухня, фартук (ст. А); по раскладке 4 шт (S = 1,11 м²), с запасом 5 шт
15	Керамогранит матовый R11, тон V486, водопоглощение 0,5 % (BIa), противоскольжение R11, PEI IV	аналог по характеристикам			м²	4,07		13. Балкон 1, пол; раскладка не выполнена — S = 3,70 м² + 10 %; клей и затирка — по раскладке
16	Плинтус из керамогранита пола, подрезка 80 мм, верхняя кромка с запилом 45°	аналог по характеристикам			м²	8,46		13. Балкон 1, стены; раскладка не выполнена — S = 7,69 м² + 10 %; клей и затирка — по раскладке
	Напольные покрытия							
17	Дуб натуральный брашированный, масло-воск, 14/4 мм, эмиссия E1, укладка на клей	аналог по характеристикам			м²	89,3		пом. 1, 3, 4, 6, 8, 9, 11, 12; S = 83,45 м² + 7 % (прямая укладка); к заказу — кратно упаковке
18	Клей для паркета и инженерной доски, эластичный (СМП / полиуретановый)	по рекомендации производителя доски			м²	84		площадь приклейки; расход и шпатель — по ТУ клея
	Погонажные изделия							
19	Плинтус МДФ под окраску 80×16 мм, крепление к стене, окраска в цвет Tikkurila F497	аналог по характеристикам			м	99		пом. 1, 3, 4, 6, 8, 9, 11, 12; L = 89,2 м (периметр без дверных проёмов) + 10 % на подрезку; в штуках — по длине планки
20	Плинтус МДФ под окраску 80×16 мм, крепление к стене, окраска в цвет Tikkurila J484	аналог по характеристикам			м	19		пом. 5, 7; L = 16,8 м (периметр без дверных проёмов) + 10 % на подрезку; в штуках — по длине планки
21	Плинтус из керамогранита пола, подрезка 80 мм, верхняя кромка с запилом 45°, h = 80 мм, крепление к стене	аналог по характеристикам			м	9		пом. 13; L = 7,7 м (периметр без дверных проёмов) + 10 % на подрезку; в штуках — по длине планки
	Смеси и материалы для облицовки							
22	Затирка для швов плитки, класс CG2WA по EN 13888	аналог: Mapei Ultracolor 133		аналог:	кг	5,7		по раскладке (a+b)/(a·b) × шов × t × 1,6 + 10 %; в т. ч. 0,1 кг — позиции раскладки без марки
23	Клей плиточный C2 TE S1 по EN 12004, слой 5 мм	аналог: Litokol K80 Eco		аналог:	кг	434		18 меш. по 25 кг; 1,5 кг/м² на 1 мм слоя + 10 %; в т. ч. 10 кг — позиции раскладки без марки
24	Гидроизоляция обмазочная мокрых зон: пол, стены по периметру, зоны замачивания; 2 слоя с армирующей лентой в углах	аналог по характеристикам			м²	16,2		площадь по листу раскладки плитки + 10 %; расход смеси — по ТУ
25	Лента демпферная по периметру пола из плитки	аналог по характеристикам			м	29,1		периметр без дверных проёмов + 10 %

Примечания

1. Количества — из геометрии проекта: площади поверхностей по чистым граням стен до отделки (те же, что в ведомости отделки и колерной карте), плитка, клей и затирка — по раскладке плиточника; в графе «Кол.» — к заказу, с запасом.
2. Краска: расход 0,12 л/м² на слой в 2 слоя, если по ТУ не задан иной; запас 10 % и 0,5 л на подкраску каждого кода. Один код — одна партия, колеровка машинная в колеровочном центре бренда; в заказ — только после утверждения выкраса (колерная карта). Фасовка — по каталогу бренда на дату выпуска; к заказу — не меньше расчётного объёма.
3. «Аналог по характеристикам» — допускается изделие другого производителя с характеристиками не ниже указанных, по согласованию с автором проекта.
4. Графы «Код продукции» и «Масса 1 ед.» не заполнены: коды по классификатору продукции не присвоены, масса единицы до 25 кг (ГОСТ 21.110-2013).
5. Грунтовка и клей для доски указаны площадью обработки; объём — по ТУ выбранного продукта.

					Проект: Четырёхкомнатная квартира		
	Лист	№ док.	Подпись	Дата	Спецификация отделочных материалов	Стадия	Лист	Листов
Дизайнер	Кырлан А.С.			04.11.26		П	С5	120

Список покупок: материалы для магазина

№	Что купить	Артикул или характеристика	Нужно с запасом	Брать в магазине	Фасовка	Уточнить в магазине	Помещения	Кто покупает
Покрытия полов и облицовка								
1	Инженерная доска (дуб натуральный, рабочий слой 4 мм, эмиссия E1, прямая укладка)	по характеристике: дуб натуральный брашированный, масло-воск, 14/4 мм	89,94 м²	90 м²		уточнить в магазине: м² в упаковке	1, 3, 4, 6, 8, 9, 11, 12	по проекту
2	Клей для паркетной и инженерной доски (эластичный, по ТУ изготовителя доски)	на выбор бригады по проекту	84,06 м²			уточнить в магазине: расход и фасовку — по выбранному продукту		бригада
3	Керамогранит 600,8×600,8 мм матовый R10, тон J484	керамогранит матовый R10, тон J484	29 шт	29 шт		уточнить в магазине: штук в коробке	2, 10	по проекту
4	Керамогранит 600,8×600,8 мм матовый, тон F497	по характеристике: керамогранит матовый, тон F497	178 шт	180 шт		уточнить в магазине: штук в коробке	2, 6, 10	по проекту
5	Керамогранит 600,8×600,8 мм матовый R10, тон V486	керамогранит матовый R10, тон V486	43 шт	44 шт		уточнить в магазине: штук в коробке	5, 7	по проекту
6	Керамогранит, R11	по характеристике: керамогранит матовый R11, тон V486, 600×600×10 мм	4,11 м²	4,2 м²		уточнить в магазине: м² в коробке	13	по проекту
Сухие смеси и гидроизоляция								
7	Клей плиточный цементный класса C2 TE S1 (ГОСТ Р 56387-2018)	аналог: Litokol K80 Eco или аналог	433,74 кг	18 меш.	мешок 25 кг			по проекту
8	Затирка цементная класса CG2WA, цвет — по колерной карте	аналог: Mapei Ultracolor 133 или аналог	5,69 кг	3 упак.	упак. 2 кг			по проекту
9	Гидроизоляция обмазочная полимерная, 2 слоя, лента в углах, манжеты на выводах	на выбор бригады по проекту	16,21 м²			уточнить в магазине: расход и фасовку — по выбранному продукту	2, 10	бригада
10	Лента демпферная по периметру пола из плитки	на выбор бригады по проекту	29,06 м	30 м		уточнить в магазине: фасовку		бригада
11	Смесь цементно-песчаная для стяжки М200 (55 мм, 53 мм)	на выбор бригады по проекту	5,55 м³			уточнить в магазине: расход и фасовку — по выбранному продукту		бригада
12	Смесь штукатурная гипсовая для машинного и ручного нанесения по маякам, слой до 10 мм	на выбор бригады по проекту	350,99 м²			уточнить в магазине: расход и фасовку — по выбранному продукту	1, 2, 3, 4, 5, 6, 7, 8, 9, 10, 11, 12, 13	бригада
Короба из ГКЛВ								
13	Лист ГКЛВ 12,5 мм, 2500 × 1200 мм, обшивка коробов в 2 слоя	на выбор бригады по проекту	6,86 м²	3 лист.	лист 3,00 м²		2, 10	бригада
14	Профиль стальной оцинкованный 27 × 28 мм: каркас коробов (стойки и направляющие)	на выбор бригады по проекту	16,69 м	6 шт	хлыст 3 м			бригада
Слаботочные сети								
15	Кабель коаксиальный RG-6 (75 Ом) к розеткам ТВ	на выбор бригады по проекту	14,5 м	15 м		уточнить в магазине: длину бухты		бригада
16	Кабель U/UTP кат. 6 (LAN, Wi-Fi и камеры по PoE)	на выбор бригады по проекту	72,7 м	73 м		уточнить в магазине: длину бухты		бригада
17	Гофротруба Ø20 для слаботочных линий, отдельно от силовых	на выбор бригады по проекту	78,5 м	79 м		уточнить в магазине: длину бухты		бригада
18	Розетка компьютерная RJ45, кат. 6, с рамкой и подрозетником	на выбор бригады по проекту	4 шт	4 шт	шт			бригада
19	Розетка телевизионная (коаксиальная) с рамкой и подрозетником	на выбор бригады по проекту	1 шт	1 шт	шт			бригада
20	Щит слаботочный ЩС: корпус, DIN-рейка, розетки 220 В	на выбор бригады по проекту	1 шт	1 шт	шт			бригада
21	Патч-панель, портов не менее 6	на выбор бригады по проекту	1 шт	1 шт	шт			бригада

					Проект: Четырёхкомнатная квартира	
	Лист	№ док.	Подпись	Дата		
Дизайнер	Кырлан А.С.			04.11.26	Список покупок	Стадия: П; Лист: С6; Листов: 120

Список покупок: материалы для магазина (продолжение)

№	Что купить	Артикул или характеристика	Нужно с запасом	Брать в магазине	Фасовка	Уточнить в магазине	Помещения	Кто покупает
Лакокрасочные материалы								
22	Краска интерьерная акриловая, матовая, класс истирания 2	Tikkurila Optiva 5 Matt L481 «Silhouette»	9,77 л	4 банк.	банка 2,7 л		1, 11	по проекту
23	Краска интерьерная акриловая, матовая, класс истирания 2	Tikkurila Optiva 5 Matt F497 «Paper»	24,89 л	10 банк.	банка 2,7 л		1, 3, 8, 11, 12	по проекту
24	Краска интерьерная акриловая, глубокоматовая, класс истирания 2	Tikkurila Anti-Reflex 2 F497 «Paper»	21,27 л	8 банк.	банка 2,7 л		1, 3, 4, 5, 7, 8, 9, 11, 12	по проекту
25	Краска интерьерная акриловая, матовая, класс истирания 1	Tikkurila Luja 7 F497 «Paper»	6,8 л	3 банк.	банка 2,7 л		2, 6, 10, 13	по проекту
26	Краска интерьерная акриловая, полуматовая, класс истирания 2	Tikkurila Joker F497 «Paper»	18,27 л	7 банк.	банка 2,7 л		4, 9	по проекту
27	Краска интерьерная акриловая, полуматовая, класс истирания 2	Tikkurila Optiva 20 Semimatt J484 «Castle»	12,14 л	5 банк.	банка 2,7 л		5, 7	по проекту
28	Краска интерьерная акриловая, полуматовая, класс истирания 1	Tikkurila Luja 7 F497 «Paper»	13,46 л	5 банк.	банка 2,7 л		6, 13	по проекту
29	Шпаклёвка финишная полимерная под окраску (стены и потолки, Q3)	на выбор бригады по проекту	430,68 м²			уточнить в магазине: расход и фасовку — по выбранному продукту		бригада
30	Грунтовка акриловая глубокого проникновения, 2 слоя	на выбор бригады по проекту	468 м²			уточнить в магазине: расход и фасовку — по выбранному продукту		бригада
Погонажные изделия и потолки								
31	Плинтус напольный МДФ под покраску, h=80 мм, крепление к стене	по характеристике: плинтус МДФ под окраску 80×16 мм	116,56 м.п.	49 шт	хлыст 2,4 м		1, 3, 4, 5, 6, 7, 8, 9, 11, 12	по проекту
32	Керамогранит на плинтус: полосы h=80 мм из плитки пола, кромка с запилом 45°	по характеристике: плинтус из керамогранита пола, подрезка 80 мм, верхняя кромка с запилом 45°	0,71 м²	0,71 м²		уточнить в магазине: м² в коробке	13	по проекту
33	Потолок подвесной ГКЛ/ГКЛВ по каркасу Knauf П113: листы, профили, подвесы, лента, шпаклёвка швов	Knauf П113	106,37 м²			уточнить в магазине: расход и фасовку — по выбранному продукту		по проекту
Инженерные изделия								
34	Мат нагревательный электрический для тёплого пола под плитку, с холодным концом и муфтой	на выбор бригады по проекту	1,67 м²			уточнить в магазине: расход и фасовку — по выбранному продукту	2, 10	по проекту
35	Терморегулятор тёплого пола с выносным датчиком пола, монтаж в подрозетник	на выбор бригады по проекту	2 шт	2 шт	шт			по проекту


Примечания

1. «Нужно с запасом» — расход по чертежам и раскладке плюс запас на подрезку и подкраску; «Брать в магазине» — то же количество в единицах, которыми продают (банки, мешки, упаковки, листы, штуки, литры).
2. «Уточнить в магазине» — фасовки этого товара в проекте нет: спросите у продавца, сколько в упаковке, и возьмите целое число упаковок не меньше «Нужно с запасом».
3. Плитку, доску и краску одного цвета берите одной партией (один калибр и тон на помещение) и сохраните чек и номер партии до конца ремонта.
4. «По характеристике» — артикул не выбран: подойдёт любой товар с этими свойствами, согласуйте его с дизайнером до покупки. «Бригада» материал выбирает и закупает бригада по своей технологии.
5. Помещения: 1 — Зал; 2 — Ванная комната; 3 — Тёмная комната; 4 — Детская 1; 5 — Коридор; 6 — Кухня; 7 — Прихожая-коридор; 8 — Гардеробная 2; 9 — Детская 2; 10 — Санузел; 11 — Гостиная; 12 — Гардеробная 1; 13 — Балкон 1; «—» — материал для нескольких помещений, расход по месту.

					Проект: Четырёхкомнатная квартира
	Лист	№ док.	Подпись	Дата	
Дизайнер	Кырлан А.С.			04.11.26	Список покупок (окончание)
					Стадия: П; Лист: С7; Листов: 120


1 Порог 15 мм: мокрая зона — смежное помещение (М 1:5)

Применение: двери

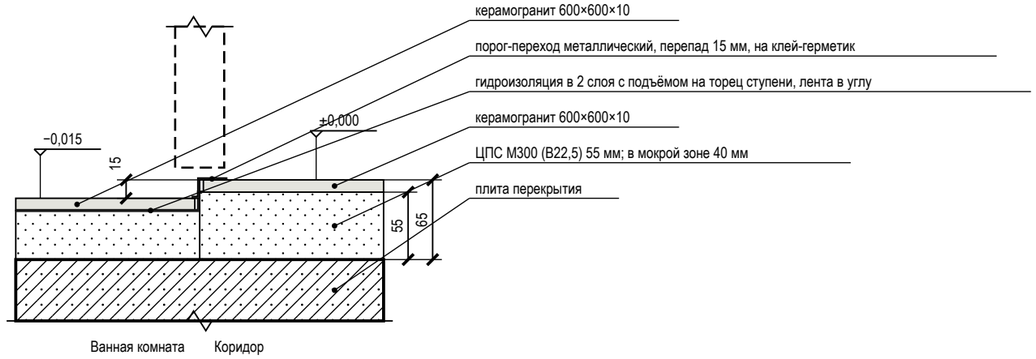


2 Стык покрытий пола Т-профилем без перепада (М 1:5)

Применение: проёмы 3↔5, 4↔5, 6↔7, 7↔8, 8↔7, 9↔7

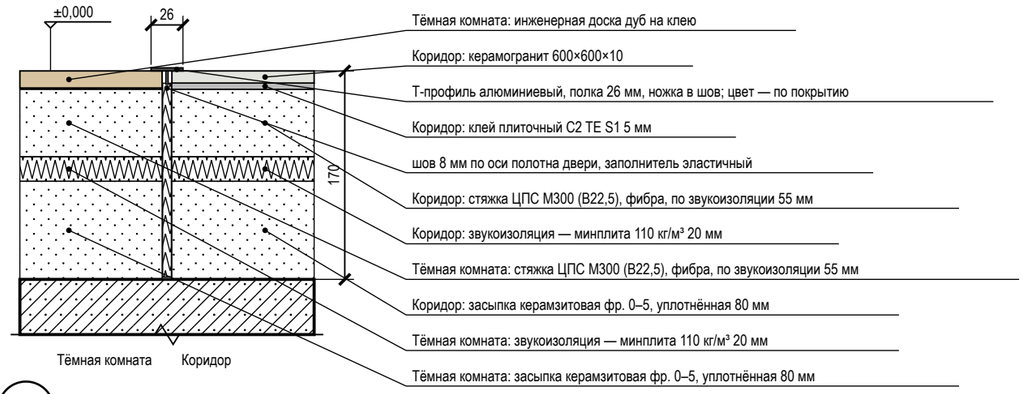


3 Короб стояков К1-1, В1-1, Т3-1 с люком и звукоизоляцией (М 1:20)

Применение: пом. 9

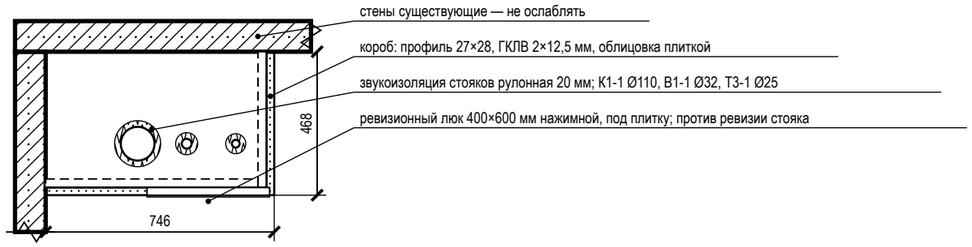


4 Гидроизоляция санузла: заход на стены 200 мм, примыкание ванны (М 1:20)

Применение: пом. 2, 10

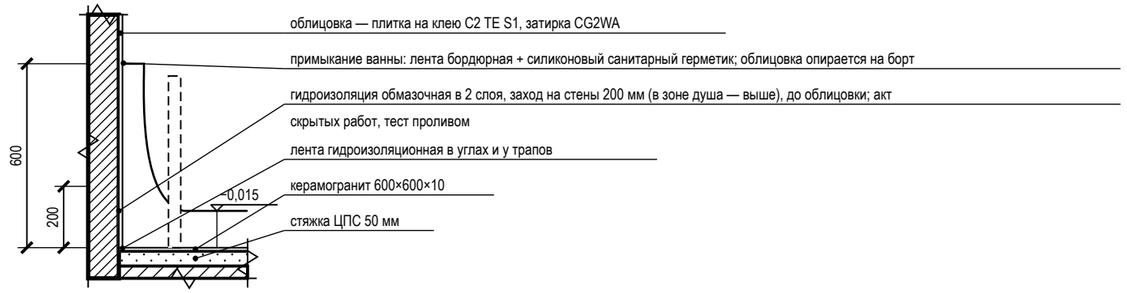


5 Плинтус МДФ 80×16 мм у окрашенной стены по доске (ламинату) (М 1:10)

Применение: пом. 1, 3, 4, 6, 8, 9, 11, 12

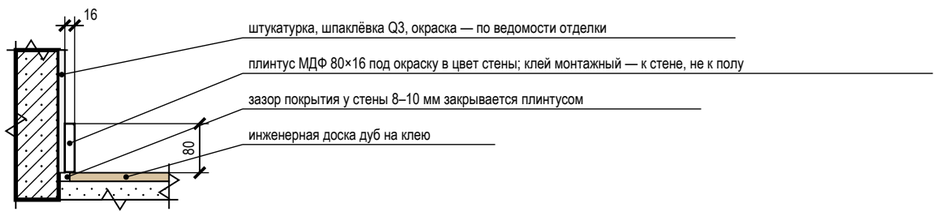

6 Плинтус МДФ 80×16 мм у окрашенной стены по керамограниту (плитке) (М 1:10)

Применение: пом. 5, 7

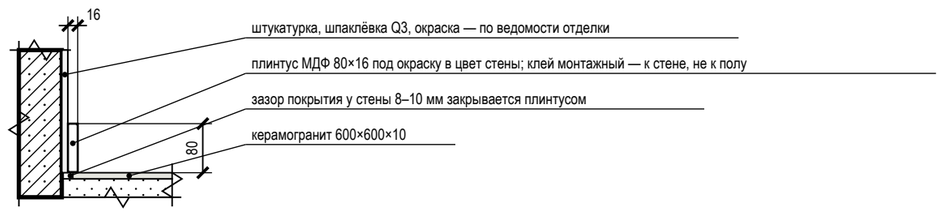

Условные обозначения

- железобетон (плита, стены) — условно: конструкция не установлена
- кладка, перегородка — условно: конструкция не установлена
- стяжка, раствор
- гипсокартон ГКЛВ
- звукоизоляция, эластичный заполнитель
- плитка, керамогранит на клею
- инженерная доска (покрытие пола)
- металлический профиль (порог, Т-профиль, короб двери)
- гидроизоляция (обмазочная, лента)

Примечания

1. Узлы — типовые решения проекта для мест, отмеченных выносками на листе схемы расположения развёрток и узлов; размеры — в мм, отметки — в м от ±0,000.
2. Узлы с гидроизоляцией, закладными и коробами скрытого монтажа принимаются по актам скрытых работ до закрытия отделкой; гидроизоляция — после теста проливом (24 ч).
3. Марки изделий (порог, Т-профиль, короб скрытой двери, люк) — по спецификациям; замена — на аналог с теми же габаритами по согласованию с автором проекта.
4. Материал плиты перекрытия и стен в узлах показан условно (железобетон, кладка): конструкция дома не установлена — крепёж, анкеры и толщины слоёв уточняются после обследования (до него — по допущениям общих указаний).

					Проект: Четырёхкомнатная квартира
	Лист	№ док.	Подпись	Дата	
Дизайнер	Кырлан А.С.			04.11.26	Узлы

Стадия	Лист	Листов
П	С8	120

выпуск 04.11.2026 № 23911fcbada · стр. 120 из 120