ДИЗАЙН-ПРОЕКТ ИНТЕРЬЕРА

# Трёхкомнатная квартира

## *Warm Contemporary*

78,95 м²

актуальность · комфорт · мягкая геометрия · контраст фактур · открытость · уверенность

Warm contemporary: потолки V503, стены Skimming Stone No. 241, грейж H487 в текстиле, один глубокий акцент Hague Blue No. 30 (изголовья спален, ТВ-стена).

ПАЛИТРА 60 / 30 / 10

| V503 | F&B No. 241 | H487 | F&B No. 30 |
|---|---|---|---|
| 60 % | 60 % | 30 % | 10 % |

Визуализация 1 · Вид сверху (3D): планировка с мебелью, текстилем и декором

| ОБЪЕКТ | ОБЩАЯ ПЛОЩАДЬ | ПОМЕЩЕНИЙ |
|---|---|---|
| Трёхкомнатная квартира | 78,95 м² | 8, из них жилых 3 |
| **СТИЛЬ** | **СТАДИЯ** | **ШИФР** |
| Современный (контемпорари) · warm contemporary | Рабочий проект | ГД-2026-003-АИ |

АВТОР ПРОЕКТА

Кырлан Александр Сергеевич

Октябрь 2026

| | | | | | Проект: Трёхкомнатная квартира | | | |
|---|---|---|---|---|---|---|---|---|
| | Лист | № док. | Подпись | Дата | Титульный лист | Стадия | Лист | Листов |
| Дизайнер | Кырлан А.С. | | | 05.10.26 | | П | 1 | 89 |

выпуск 05.10.2026 № 6a37468da7 · стр. 1 из 89

## Список листов


| Лист | Наименование |
|---|---|
| 1 | Титульный лист |
| 2 | Список листов |
| 3 | План планировки от заказчика |
| 4 | План монтажный |
| 5 | Схема каркаса перегородки П-1 |
| 6 | Кухня (пом. 6). Монтажная схема |
| 7 | Шкафы. Монтажная схема |
| 8 | Карта покрытий стен |
| 9 | Колерная карта |
| 10 | План размещения мебели и оборудования |
| 11 | Спецификация мебели и оборудования |
| 12 | Спецификация мебели и оборудования (продолжение) |
| 13 | Ведомости изделий, техники и фурнитуры |
| 14 | План выводов сантехники |
| 15 | Схема разводки водопровода и канализации |
| 16 | Спецификация сантехнического оборудования |
| 17 | Раскладка плитки. Ванная. Развёртки стен |
| 18 | Раскладка плитки. Санузел 2. Развёртки стен |
| 19 | План размещения дверей |
| 20 | План потолков |
| 21 | Разрезы и узлы потолков |
| 22 | План розеток и электровыводов |
| 23 | План слаботочных сетей |
| 24 | План освещения |
| 25 | Спецификация светильников и сценарии освещения |
| 26 | Управление светильниками |
| 27 | План вентиляции |
| 28 | План отопления |
| 29 | План покрытий пола |
| 30 | Раскладка плитки. Планы полов |
| 31 | Раскладка плитки. Прихожая. Фартук кухни |
| 32 | Визуализация. Вид сверху |
| 33 | Визуализация |
| 34 | Визуализация: Спальня 1 |
| 35 | Визуализация: Спальня 1 |
| 36 | Визуализация: Спальня 1 |
| 37 | Развёртка стены А. Спальня 1 (пом. 1) |
| 38 | Развёртка стены Б. Спальня 1 (пом. 1) |
| 39 | Развёртка стены В. Спальня 1 (пом. 1) |
| 40 | Развёртка стены Г. Спальня 1 (пом. 1) |
| 41 | Визуализация ванной |
| 42 | Визуализация ванной |
| 43 | Визуализация ванной |
| 44 | Визуализация ванной |
| 45 | Развёртки стен А, Б. Ванная (пом. 2) |
| 46 | Развёртка стены В. Ванная (пом. 2) |
| 47 | Развёртка стены Г. Ванная (пом. 2) |
| 48 | Визуализация гардеробной |
| 49 | Развёртки стен. Гардеробная (пом. 3) |
| 50 | Визуализация: Спальня 2 |
| 51 | Визуализация: Спальня 2 |
| 52 | Визуализация: Спальня 2 |
| 53 | Развёртка стены А. Спальня 2 (пом. 4) |
| 54 | Развёртка стены Б. Спальня 2 (пом. 4) |
| 55 | Развёртка стены В. Спальня 2 (пом. 4) |
| 56 | Развёртка стены Г. Спальня 2 (пом. 4) |
| 57 | Визуализация прихожей |
| 58 | Визуализация прихожей |
| 59 | Развёртка стены А. Прихожая (пом. 5) |
| 60 | Развёртка стены Б. Прихожая (пом. 5) |
| 61 | Развёртка стены В. Прихожая (пом. 5) |
| 62 | Развёртка стены Г. Прихожая (пом. 5) |
| 63 | Визуализация кухни-гостиной |
| 64 | Визуализация кухни-гостиной |
| 65 | Визуализация кухни-гостиной |
| 66 | Визуализация кухни-гостиной |
| 67 | Визуализация кухни-гостиной |
| 68 | Визуализация кухни-гостиной |
| 69 | Развёртка стены Б2. Кухня-гостиная (пом. 6), кухонный фронт |
| 70 | Развёртка стены В1. Кухня-гостиная (пом. 6), кухонный фронт |
| 71 | Развёртка стены А. Кухня-гостиная (пом. 6) |
| 72 | Развёртка стены Б1. Кухня-гостиная (пом. 6) |
| 73 | Развёртки стен В2, Г1. Кухня-гостиная (пом. 6) |
| 74 | Развёртка стены Г2. Кухня-гостиная (пом. 6) |
| 75 | Визуализация: Санузел 2 |
| 76 | Визуализация: Санузел 2 |
| 77 | Развёртки стен А, Б. Санузел 2 (пом. 7) |
| 78 | Развёртки стен В, Г. Санузел 2 (пом. 7) |
| 79 | Визуализация коридора |
| 80 | Визуализация коридора |
| 81 | Развёртки стен А, Б. Коридор (пом. 8) |
| 82 | Развёртки стен В, Г. Коридор (пом. 8) |
| Д_1 | Шкаф распашной М_05 |
| Д_2 | Система хранения М_07 |
| Д_3 | Шкаф-купе М_13 |
| Д_4 | Кухня (пом. 6). Развёртка гарнитура |
| С1 | Ведомость отделки помещений |
| С2 | Спецификация отделочных материалов |
| С3 | Узлы |


## Общие указания

1. Размеры даны в мм от чистовых поверхностей стен: слой штукатурки 20 мм по блоку и 5 мм шпаклёвки по ГКЛ учтён. Перед заказом встроенной мебели — контрольный обмер после штукатурки.
2. Привязки мебели — от стен и углов помещения, а не от другой мебели.
3. Розетки, выводы и выключатели под мебель — см. лист 22 «План розеток и электровыводов»; сантехприборы и выводы воды — лист 14.
4. План расстановки не является документацией для изготовления мебели: изделия — по чертежам мебельщика; покупную мебель заменять только на изделия не больше габарита из спецификации (лист 11).
5. Встроенная мебель «стена в стену» — с зазором 10 мм с каждой стороны или с компенсаторами.
6. Развёртки — вид на стену изнутри помещения, по часовой стрелке; расположение стен на схеме листа развёртки; размеры — в мм по чистовым поверхностям; отметки — в м от ±0,000; высоты H — от чистого пола помещения до оси изделия, у декора — до центра.
7. Красные цепочки — привязки электроточек и выводов: по горизонтали от угла чистовых стен, по вертикали от чистого пола, до оси изделия; звенья короче 3 мм на листе вынесены во второй ярус (ближняя к стене цепочка).
8. У знака электроточки: марка (Р — розетка, S — выключатель, Св — светильник, ЭВ вывод кабеля), ×N — число постов в рамке, гр. — группа щита, H — высота оси от чистого пола, мм; группы по клавишам выключателя — на листе выключателей.
9. Схема мебели, приборов и декора не является технической документацией для производства мебели; габариты — по паспортам изделий.
10. Марки позиций: М_NN — мебель, ОБ_NN — оборудование, С_NN — сантехника; О-N отделка (ведомость отделочных материалов, серия С).
11. Размеры мебели и изделий на заказ уточнить по месту после отделочных работ.

| | | | | |
|---|---|---|---|---|
| | Лист | № док. | Подпись | Дата |
| Дизайнер | Кырлан А.С. | | | 05.10.26 |

Проект: Трёхкомнатная квартира

Список листов

| Стадия | Лист | Листов |
|---|---|---|
| П | 2 | 89 |

выпуск 05.10.2026 № 6a37468da7 · стр. 2 из 89

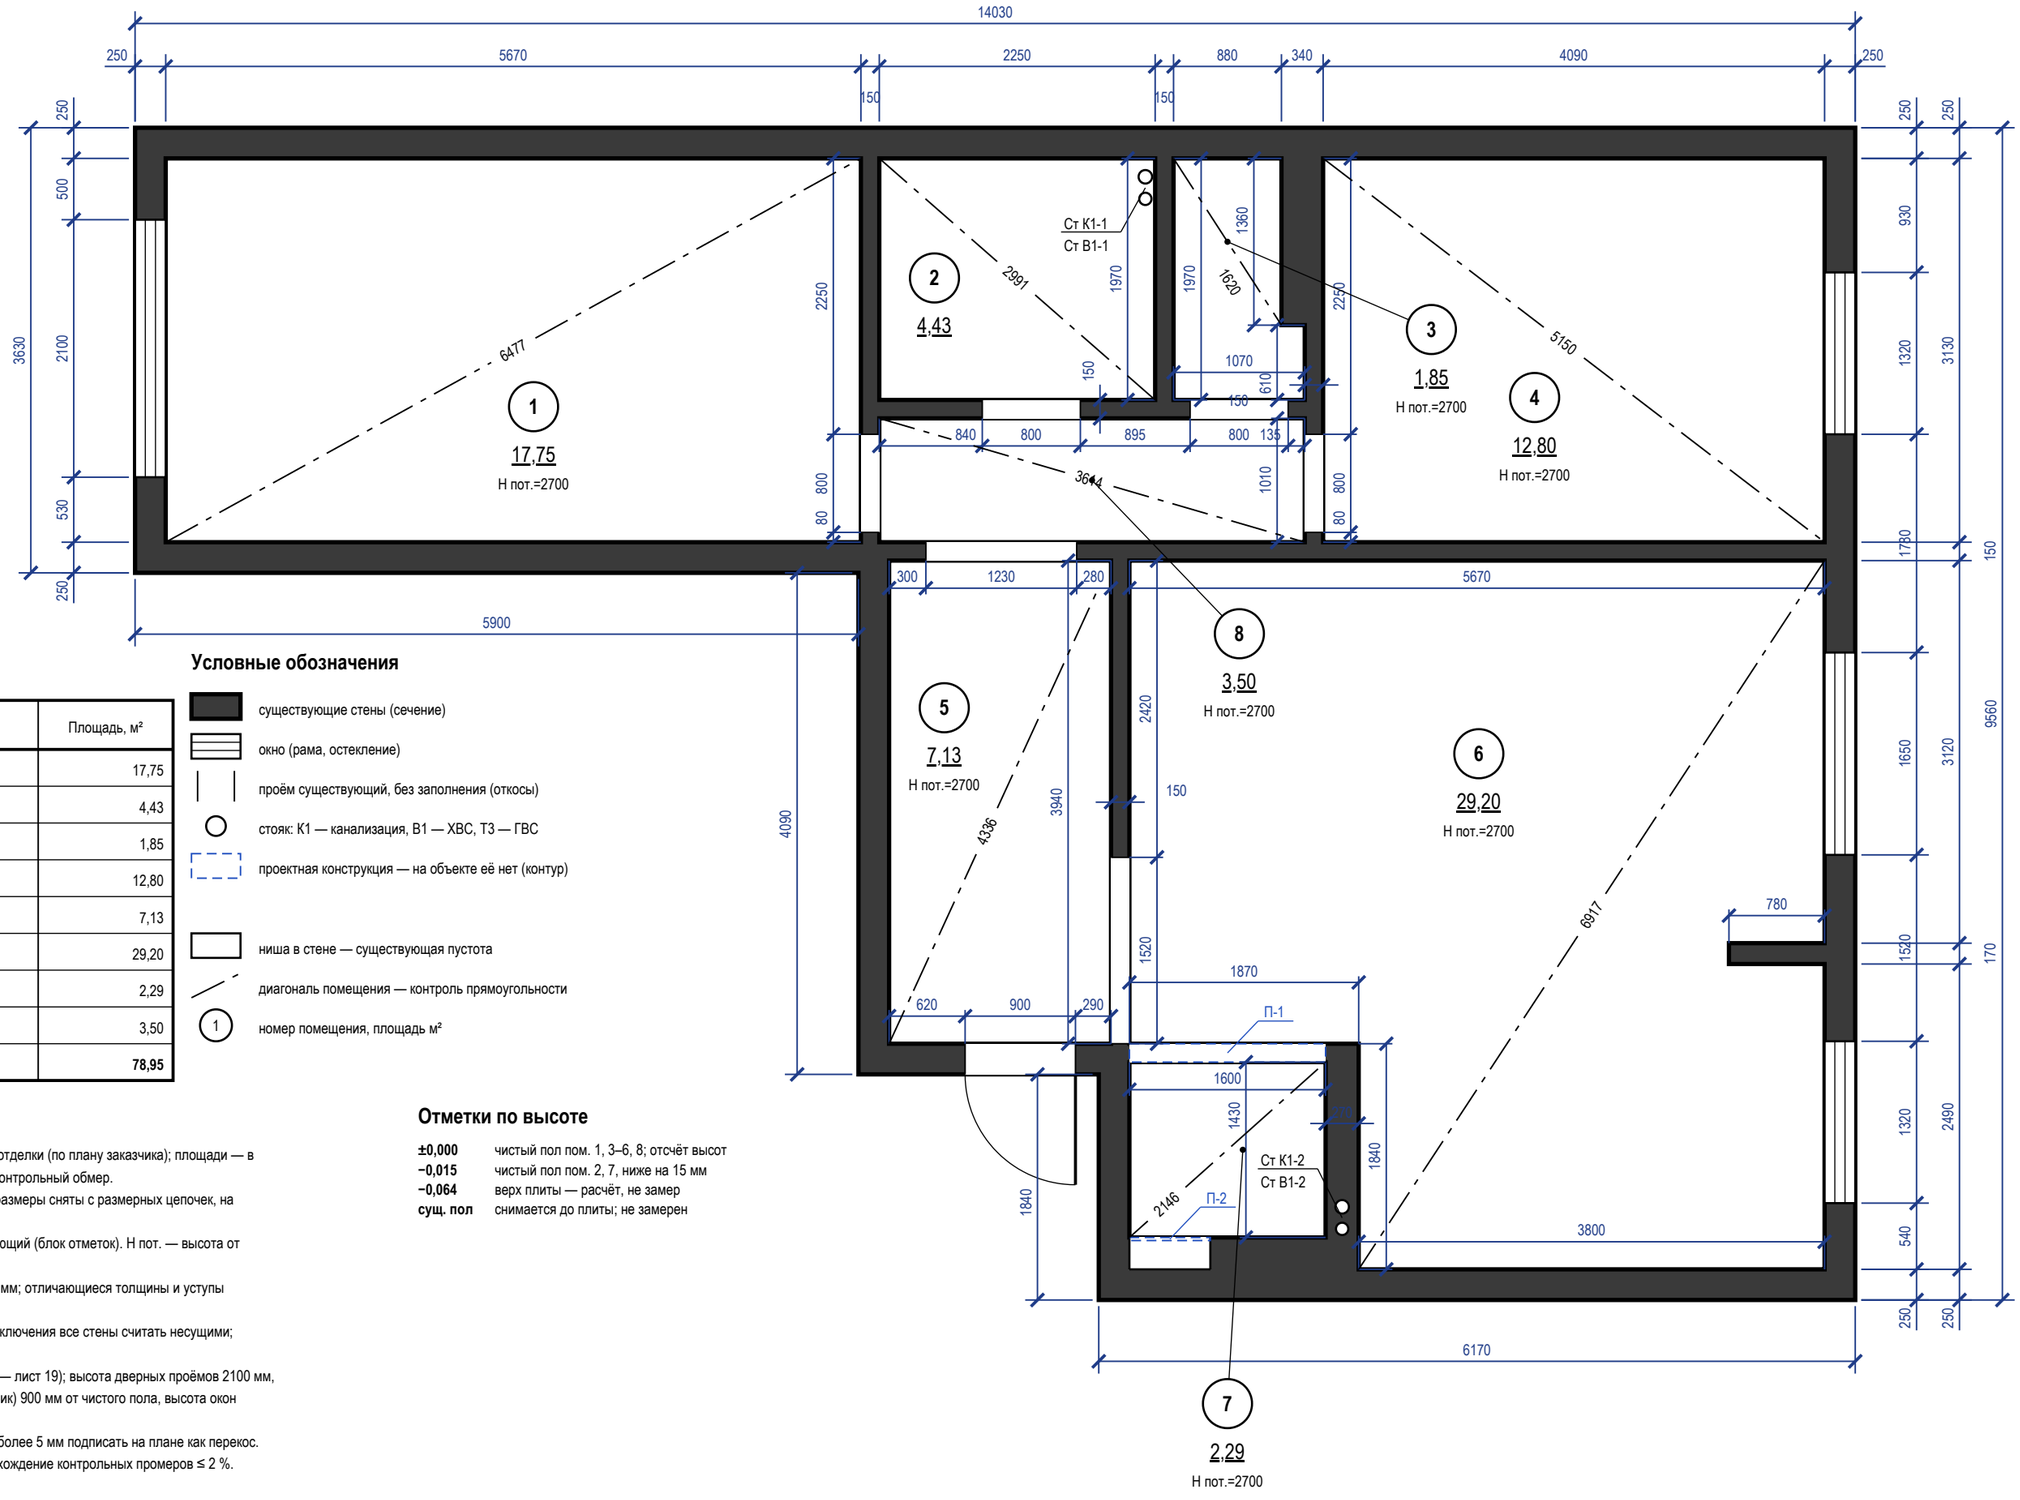


## Экспликация помещений

| № | Наименование | Площадь, м² |
|---|---|---|
| 1 | Спальня 1 | 17,75 |
| 2 | Ванная | 4,43 |
| 3 | Гардеробная | 1,85 |
| 4 | Спальня 2 | 12,80 |
| 5 | Прихожая | 7,13 |
| 6 | Кухня-гостиная | 29,20 |
| 7 | Санузел 2 | 2,29 |
| 8 | Коридор | 3,50 |
| | **Итого (общая площадь)** | **78,95** |

## Условные обозначения

- существующие стены (сечение)
- окно (рама, остекление)
- проём существующий, без заполнения (откосы)
- стояк: К1 — канализация, В1 — ХВС, Т3 — ГВС
- проектная конструкция — на объекте её нет (контур)
- ниша в стене — существующая пустота
- диагональ помещения — контроль прямоугольности
- (1) номер помещения, площадь м²

## Примечания

1. Размеры — в мм по чистым поверхностям стен до отделки (по плану заказчика); площади — в м² по тем же размерам. До начала работ выполнить контрольный обмер.
2. Источник плана: растровый скан плана заказчика, размеры сняты с размерных цепочек, на объекте не замерены.
3. За отметку ±0,000 принят чистый пол, не существующий (блок отметок). Н пот. — высота от чистого пола до плиты перекрытия.
4. Толщины стен: наружные 250 мм, перегородки 150 мм; отличающиеся толщины и уступы размерами на плане.
5. Несущие стены не определены: до технического заключения все стены считать несущими; проёмы и штробы в них не выполнять.
6. Дверные проёмы показаны без заполнения (двери — лист 19); высота дверных проёмов 2100 мм, проёмов без двери 2500, 2100 мм; низ окон (подоконник) 900 мм от чистого пола, высота окон 1500, 1400 мм.
7. Диагонали — контрольные размеры; расхождение более 5 мм подписать на плане как перекос.
8. Размеры проверить на месте до начала работ; расхождение контрольных промеров ≤ 2 %.

## Отметки по высоте

| | |
|---|---|
| **±0,000** | чистый пол пом. 1, 3–6, 8; отсчёт высот |
| **−0,015** | чистый пол пом. 2, 7, ниже на 15 мм |
| **−0,064** | верх плиты — расчёт, не замер |
| **сущ. пол** | снимается до плиты; не замерен |

| | | | | | |
|---|---|---|---|---|---|
| | | | | | Проект: Трёхкомнатная квартира |
| | Лист | № док. | Подпись | Дата | План планировки от заказчика |
| Дизайнер | Кырлан А.С. | | | 05.10.26 | Стадия: П; Лист: 3; Листов: 89 |

выпуск 05.10.2026 № 6a37468da7 · стр. 3 из 89

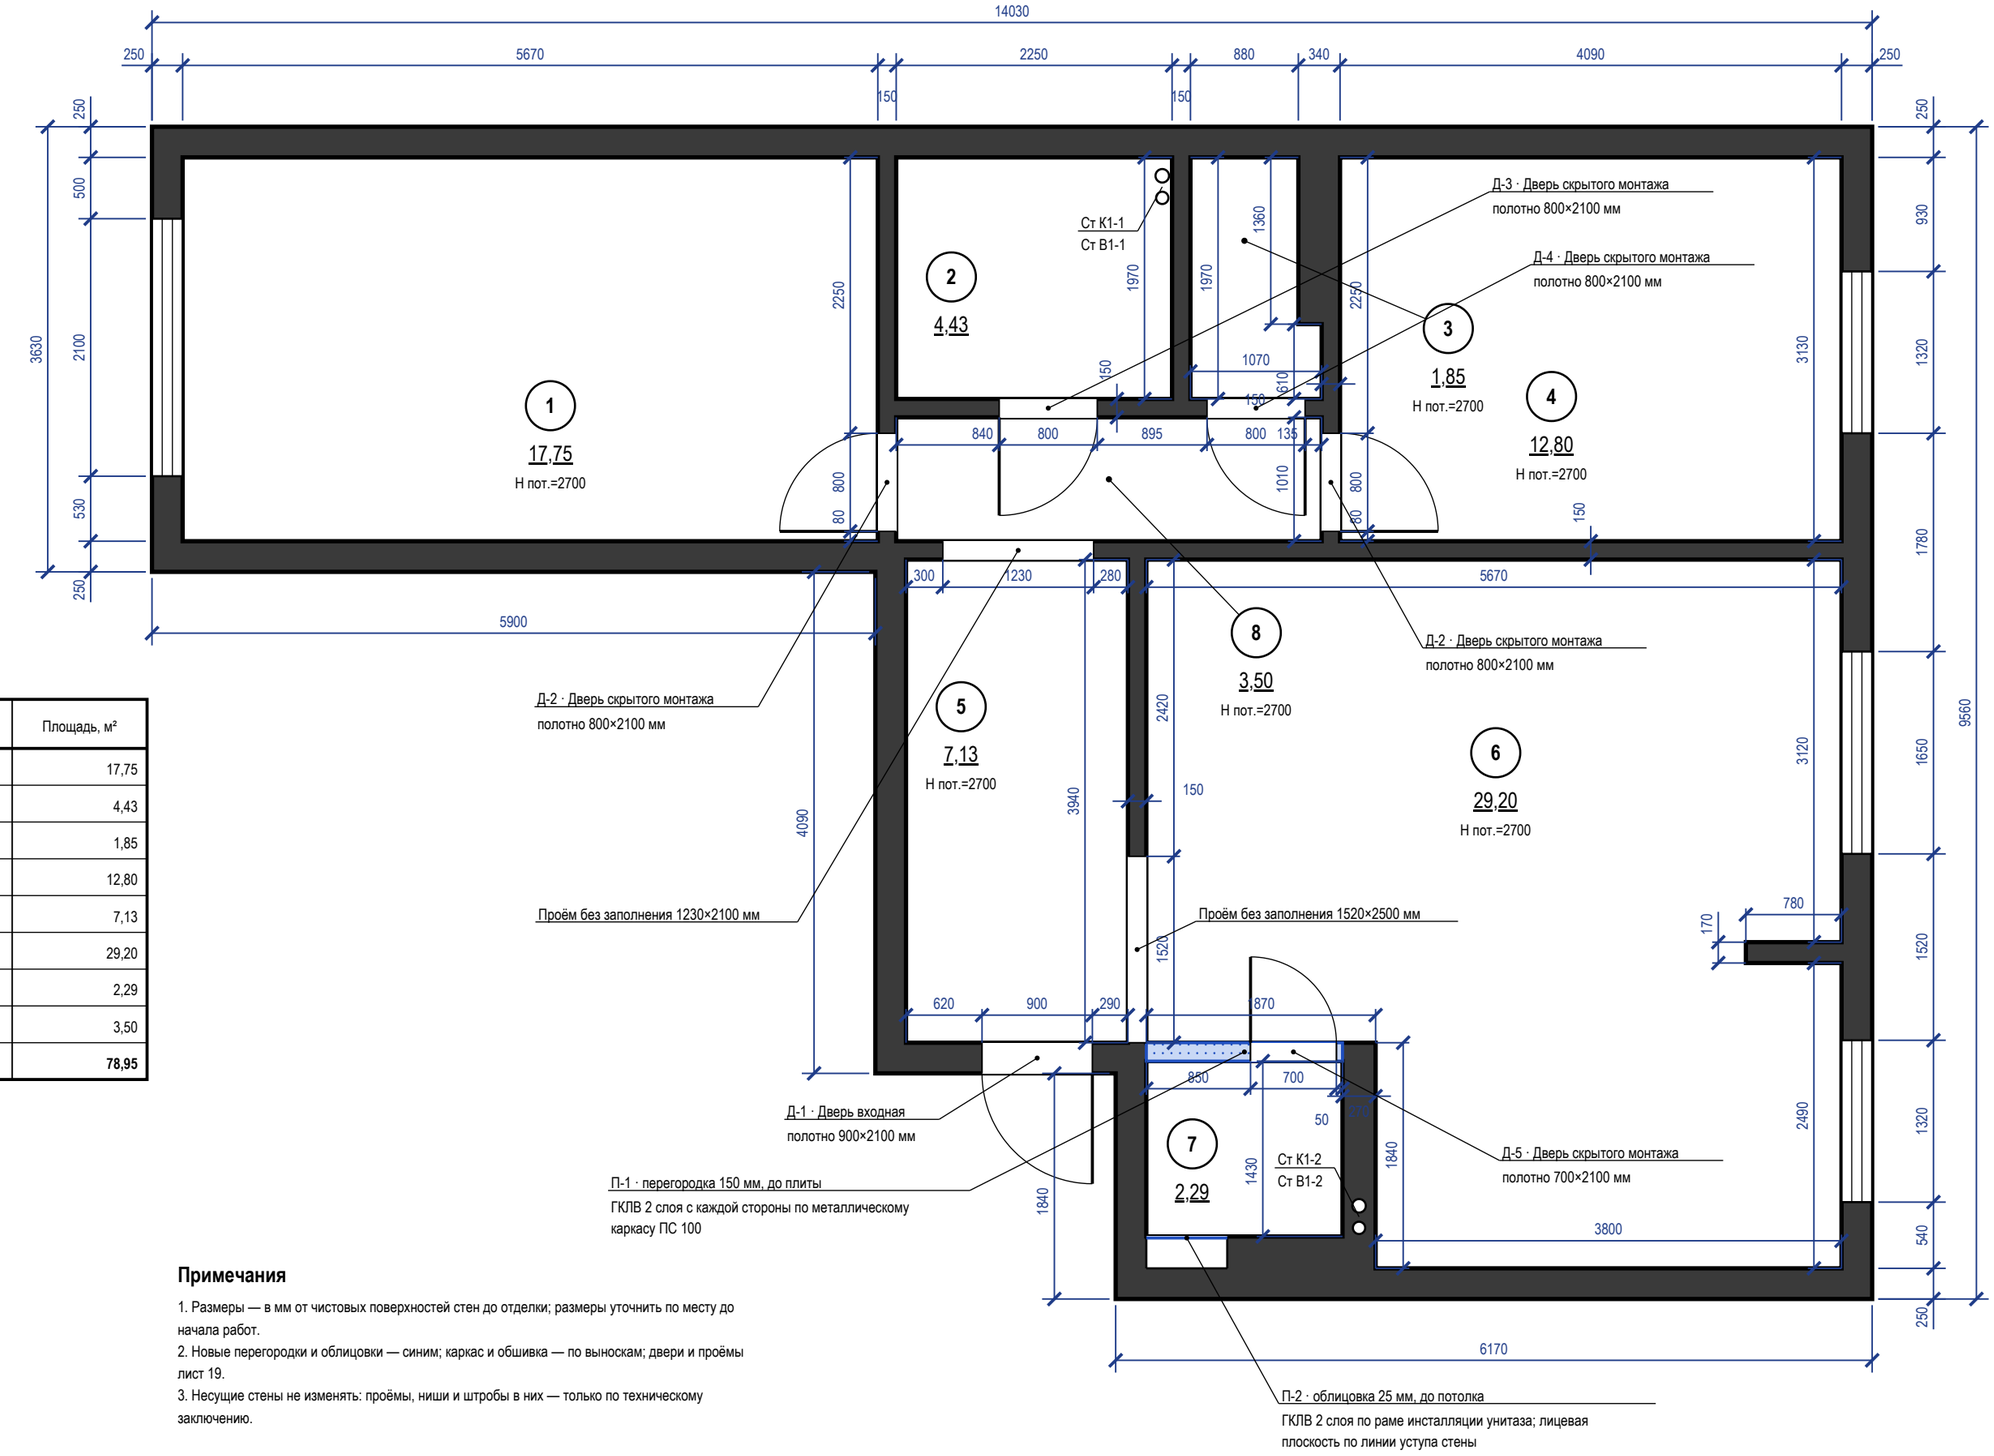


## Экспликация помещений

| № | Наименование | Площадь, м² |
|---|---|---|
| 1 | Спальня 1 | 17,75 |
| 2 | Ванная | 4,43 |
| 3 | Гардеробная | 1,85 |
| 4 | Спальня 2 | 12,80 |
| 5 | Прихожая | 7,13 |
| 6 | Кухня-гостиная | 29,20 |
| 7 | Санузел 2 | 2,29 |
| 8 | Коридор | 3,50 |
| | **Итого (общая площадь)** | **78,95** |

## Примечания

1. Размеры — в мм от чистовых поверхностей стен до отделки; размеры уточнить по месту до начала работ.
2. Новые перегородки и облицовки — синим; каркас и обшивка — по выноскам; двери и проёмы лист 19.
3. Несущие стены не изменять: проёмы, ниши и штробы в них — только по техническому заключению.

| | | | | | |
|---|---|---|---|---|---|
| | | | | | Проект: Трёхкомнатная квартира |
| | Лист | № док. | Подпись | Дата | План монтажный |
| Дизайнер | Кырлан А.С. | | | 05.10.26 | |

| Стадия | Лист | Листов |
|---|---|---|
| П | 4 | 89 |

выпуск 05.10.2026 № 6a37468da7 · стр. 4 из 89

## Вид на каркас без обшивки (М 1:20)

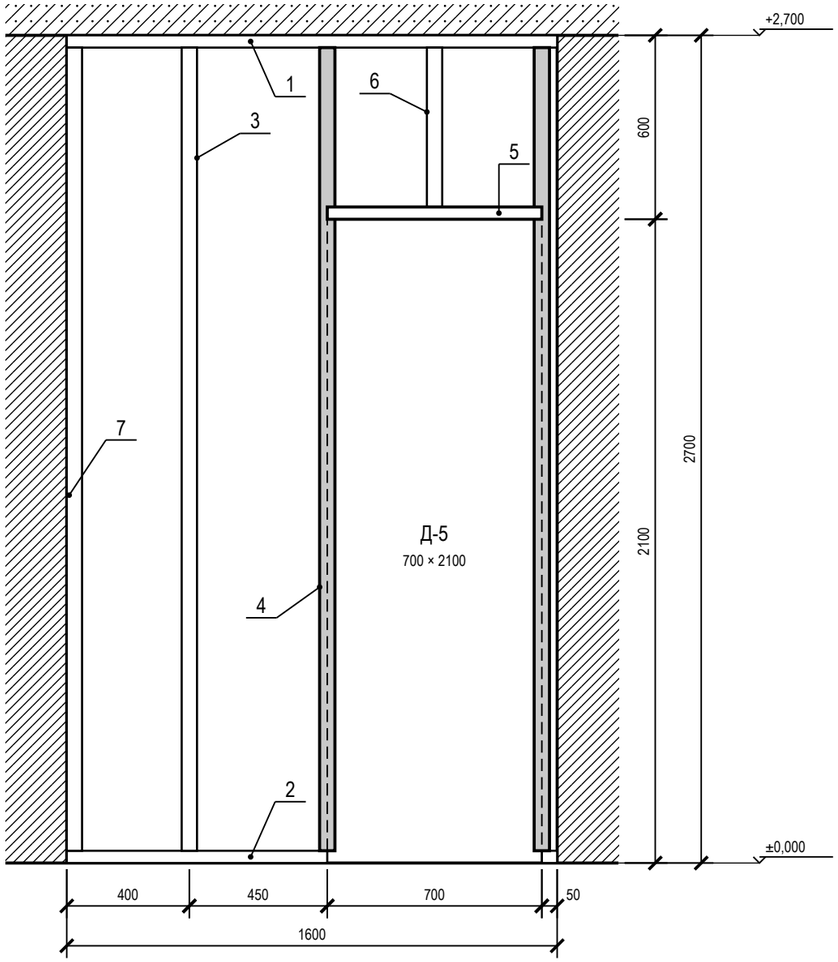


Оси — стойки каркаса; полки профиля на виде условны

## Сечение А–А по стойке (М 1:5)

сверху — пом. 6, окраска

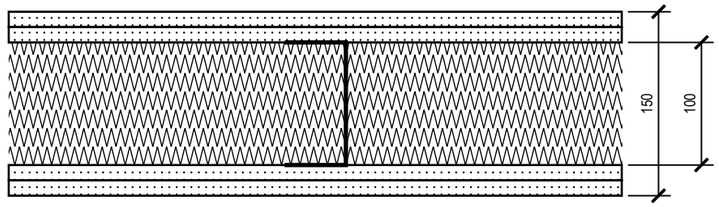


снизу — пом. 7, плитка

поз. 9 — ГКЛВ 12,5 мм в 2 слоя с каждой стороны; поз. 3 — ПС 100; поз. 8 — минвата 100 мм (принято)

## Сечение Б–Б у проёма, на уровне ниже перемычки (М 1:5)

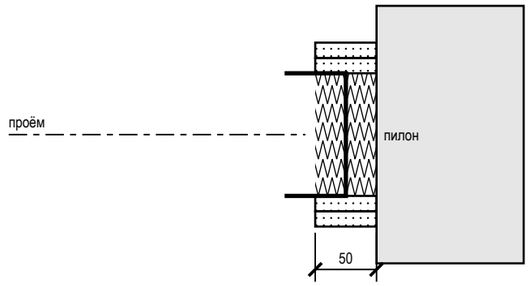


поз. 4 — УА 100, обрамление проёма; обшивка по краю проёма, простенок 50 мм до пилона

## Узел 1. К плите (М 1:5)

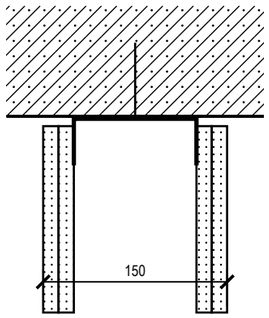


## Узел 2. К полу (М 1:5)

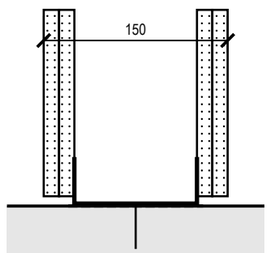


## Ведомость элементов каркаса

| Поз. | Наименование | Кол-во | Ед. |
|---|---|---|---|
| 1 | ПН 100 по потолку (по плите) | 1,60 | м |
| 2 | ПН 100 по полу, без проёма | 0,90 | м |
| 3 | ПС 100 через 400 мм | 2 × 2,70 | м |
| 4 | УА 100 по краям проёма | 2 × 2,70 | м |
| 5 | ПН 100 перемычка над проёмом | 0,70 | м |
| 6 | ПС 100 над перемычкой | 1 × 0,60 | м |
| 7 | Лента уплотнительная под профили | 7,90 | м |
| 8 | Минвата в полость, 100 мм | 2,85 | м² |
| 9 | ГКЛВ 12,5 мм, 2 слоя с двух сторон | 11,40 | м² |

Итого: ПН 3,20 м, ПС 6,00 м, УА 5,40 м; сторона 2,85 м²

## Примечания

1. П-1 (С112, ГКЛВ в 2 слоя с каждой стороны, толщина 150 мм, высота 2700 мм до плиты); ось и длина 1600 мм — со скана плана заказчика (контрольный обмер не выполнялся).
2. Шаг стоек 400 мм — по данным (под плитку и во влажной зоне). Размеры сечений профилей — «ПС 100», «УА 100» по данным и каталогу; толщины листов — ГОСТ 32614-2012.
3. Стойка ПС на 800 мм не ставится: ось в 50 мм от УА на 850 мм, два профиля с полкой 50 мм не помещаются — УА проёма служит и стойкой каркаса; полка 50 мм принята по каталогу Knauf.
4. Стойка ПС на 1600 мм не ставится: ось в 50 мм от УА на 1550 мм, два профиля с полкой 50 мм не помещаются — УА проёма служит и стойкой каркаса у конца перегородки; полка 50 мм принята по каталогу Knauf.
5. Проём Д-5 в каркасе 700 × 2100 мм принят по размеру полотна: короб скрытой двери (модель, размеры) не выбран — проём пересчитать по коробке до монтажа УА.
6. Перемычка над проёмом — направляющий профиль по верху проёма на всю его ширину; короткие стойки ПС над перемычкой на шаге каркаса: по практике узла Knauf, не по данным объекта.
7. Заполнение полости — минераловатная плита на всю глубину профиля (Rw системы С112 нормируют с заполнением); марка и плотность выбираются при закупке.
8. Длина стойки равна высоте перегородки: стойки режут на высоту между направляющими при монтаже, зазоры до плиты и пола в данных не заданы (edgeGaps).
9. Простенок 50 мм между проёмом Д-5 и концом перегородки: УА проёма — последняя стойка в 50 мм от примыкания, полоса обшивки в 50 мм уже удобной ширины; решение по положению проёма — за автором.
10. Обшивку крепят к стойкам шурупами через слой, швы слоёв вразбежку; зазоры обшивки до плиты и пола, шаг дюбелей, марка заполнения — по ТУ системы и узлу изготовителя.

| | | | | | Проект: Трёхкомнатная квартира | | | |
|---|---|---|---|---|---|---|---|---|
| | Лист | № док. | Подпись | Дата | Схема каркаса перегородки П-1 | Стадия | Лист | Листов |
| Дизайнер | Кырлан А.С. | | | 05.10.26 | | П | 5 | 89 |

## Привязка выводов и крепление модулей

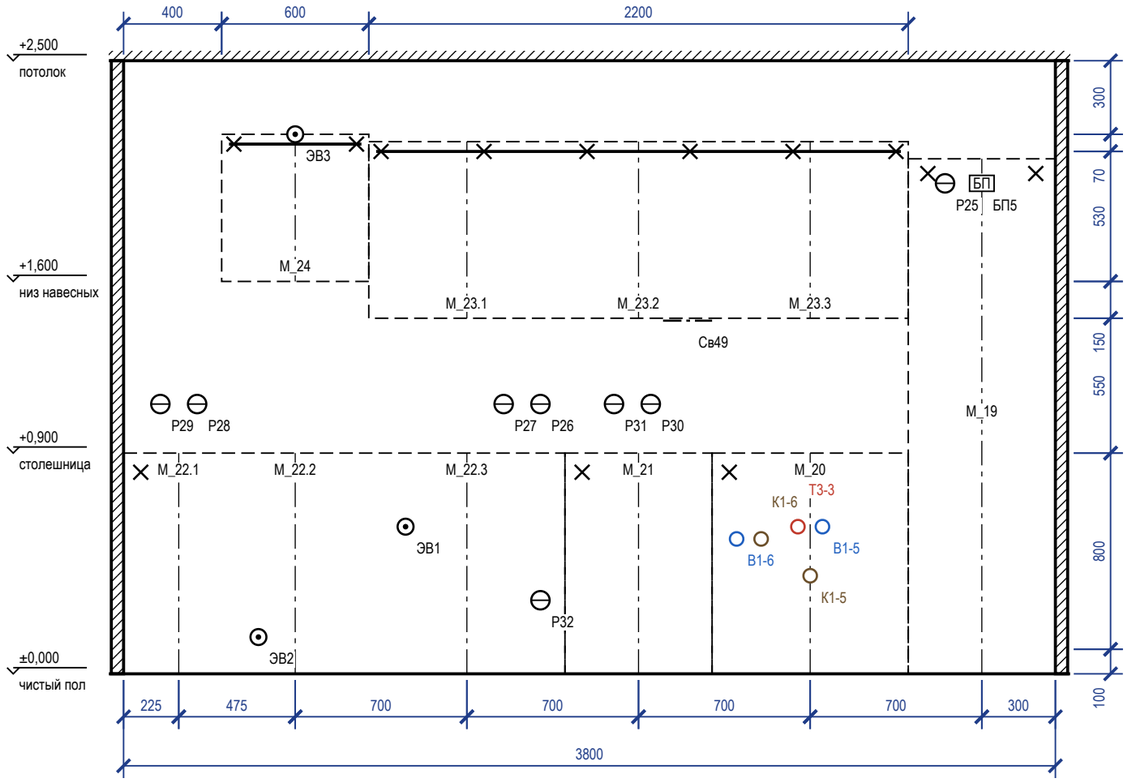


## План столешницы

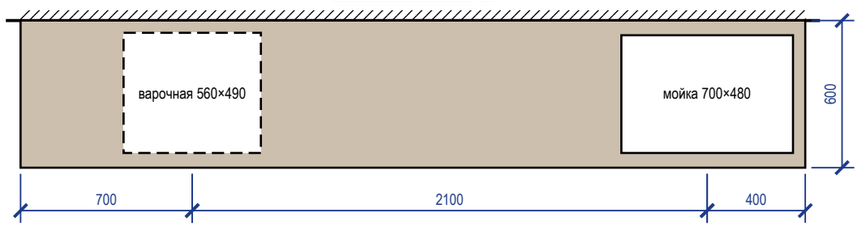


## Примечания

1. Выводы — по проекту электрики и ВК; привязка по горизонтали — от оси модуля (плюс — вправо по виду), по высоте — от чистого пола до оси вывода.
2. Пенал — уголки к стене 2 шт. сверху; нижние модули — стяжками между собой и уголком к стене; ряд выставить по уровню опорами цоколя.
3. Розетки над столешницей — не ниже 150 мм над ней и не за корпусом техники; розетка за ПММ, духовым шкафом и холодильником — только в соседнем модуле или в зоне цоколя с доступом.
4. Столешница — вырезы по шаблонам выбранных моделей мойки и варочной панели; торцы у стены — герметик, пристеночный плинтус.

## Привязка выводов к осям модулей

| Код | Назначение | Модуль | От оси, мм | Н, мм | Размещение |
|---|---|---|---|---|---|
| Р29 | розетка — фартук | М_22.1 | −75 | 1100 | над столешницей (фартук) |
| Р28 | розетка ×2 — фартук | М_22.1 | +75 | 1100 | над столешницей (фартук) |
| ЭВ2 | вывод кабеля — духовой шкаф | М_22.2 | −150 | 150 | под духовым шкафом, доступ через ящик |
| ЭВ3 | вывод кабеля — вытяжка | М_24 | 0 | 2200 | в навесном модуле |
| ЭВ1 | вывод кабеля — варочная панель (в соседнем модуле М_22.3, за ящиком) | М_22.3 | −250 | 600 | в соседнем модуле, за ящиком |
| Р27 | розетка — фартук | М_22.3 | +150 | 1100 | над столешницей (фартук) |
| Р26 | розетка ×2 — фартук | М_22.3 | +300 | 1100 | над столешницей (фартук) |
| Р32 | розетка — посудомоечная машина | М_22.3 | +300 | 300 | в соседнем модуле, за ящиком |
| Р31 | розетка — фартук между мойкой и варочной | М_21 | −100 | 1100 | над столешницей (фартук) |
| Р30 | розетка ×2 — фартук между мойкой и варочной | М_21 | +50 | 1100 | над столешницей (фартук) |
| Св49 | светодиодная лента — подсветка столешницы | М_21 | +200 | 1440 | в профиле по низу навесного модуля |
| В1-6 | В1 — кран ПММ в шкафу мойки | М_20 | −300 | 550 | в модуле мойки |
| К1-6 | К1 Ø40 — слив ПММ в шкафу мойки | М_20 | −200 | 550 | в модуле мойки |
| Т3-3 | Т3 — межос. 100 | М_20 | −50 | 600 | в модуле мойки |
| К1-5 | К1 Ø50 — мойка | М_20 | 0 | 400 | в модуле мойки |
| В1-5 | В1 — межос. 100 | М_20 | +50 | 600 | в модуле мойки |
| Р25 | розетка — холодильник, над нишей М_19 (съёмная панель) | М_19 | −150 | 2000 | над нишей холодильника, съёмная панель |
| БП5 | блок питания — в пенале М_19, верх, съёмная панель | М_19 | 0 | 2000 | над нишей холодильника, съёмная панель |

## Зазоры под отделку

| Поверхность | Отделка | Зазор, мм | Учесть |
|---|---|---|---|
| фартук | керамогранит | 10 | от чернового основания до корпуса навесных и столешницы |
| стены | окраска | 5 | под штукатурку и шпаклёвку за пеналом |
| пол | инженерная доска | | цоколь — после укладки пола, опоры ±20 мм |

## Условные обозначения

- навесной модуль (невидимый контур)
- ось модуля (от неё — привязка вывода)
- анкер / уголок крепления к стене
- розетка на стене
- вывод кабеля к технике
- В1 — вывод воды В1 / Т3, канализации К1

| | | | | | |
|---|---|---|---|---|---|
| | | | | | Проект: Трёхкомнатная квартира |
| | Лист | № док. | Подпись | Дата | Кухня (пом. 6). Монтажная схема |
| Дизайнер | Кырлан А.С. | | | 05.10.26 | |

| Стадия | Лист | Листов |
|---|---|---|
| П | 6 | 89 |

выпуск 05.10.2026 № 6a37468da7 · стр. 6 из 89

**Шкаф распашной M_05 (пом. 1)**

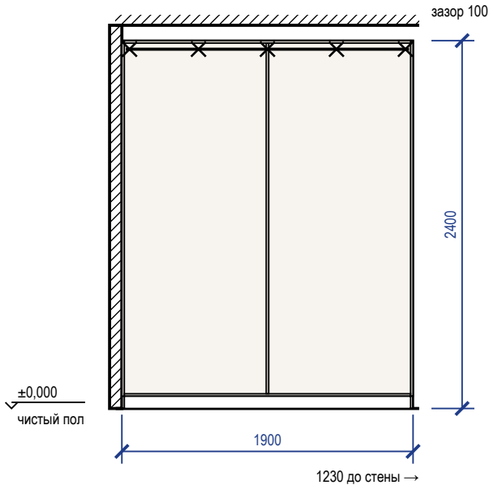


**Система хранения M_07 (пом. 3)**

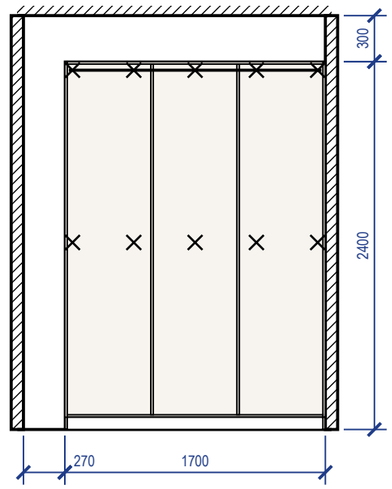


**Шкаф-купе M_13 (пом. 5)**

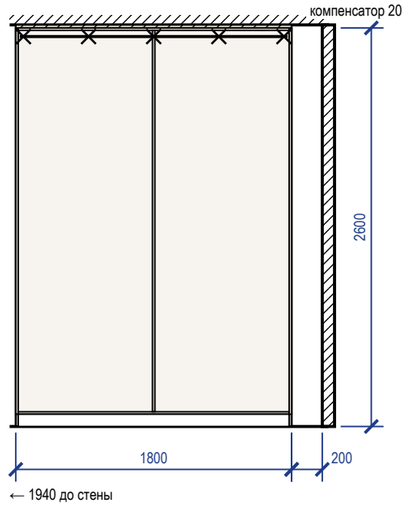


## Крепление и зазоры под отделку

| Марка | Помещение, стена | Основание | Отделка стены | Зазор, мм | Крепёж по планке | От опрокидывания |
|---|---|---|---|---|---|---|
| M_05 | Спальня 1 (1), стена Б | по основанию — см. таблицу крепежа | окраска | 5 | анкер 5 шт., шаг 450 | уголок к стене, 2 шт. |
| M_07 | Гардеробная (3), стена Г | по основанию — см. таблицу крепежа | окраска | 5 | анкер 10 шт. (2 ряда) | крепление к стене, 3 точки |
| M_13 | Прихожая (5), стена Г | по основанию — см. таблицу крепежа | окраска | 5 | анкер 5 шт., шаг 425 | уголки 2 шт. |

## Крепёж по основанию стены

| Основание стены | Крепёж |
|---|---|
| бетон, ж/б | анкер-шуруп 7,5×72 или дюбель 8×60 с шурупом 5×70 |
| кирпич полнотелый | дюбель 8×80 с шурупом 5×90 |
| газобетон, пазогребень | дюбель для газобетона 10×100 или химический анкер |
| гипсокартон | закладная до обшивки (брус 40×80 или фанера 18 мм), саморез в закладную |

## Условные обозначения

- × — анкер / уголок крепления к стене
- прямоугольник — корпус и полки ЛДСП (вид на стену)
- штриховка — компенсатор — короб до потолка

## Примечания

1. Установочные размеры — от чистого пола и чистых стен; перед установкой контрольный замер после отделки.
2. Порядок: корпус выставить по уровню опорами цоколя → закрепить к стене по задней планке → навесить двери и фасады, отрегулировать зазоры → подогнать и закрепить компенсатор.
3. Анкеры — с шагом не более 500 мм, не ближе 50 мм от края планки; на ГКЛ только в закладную, установленную до обшивки.
4. Скрытые коммуникации под анкеры проверить детектором; трассы электрики по плану розеток.
5. Сборка стоя на месте: M_13 (диагональ боковины 2668 мм > 2620 мм до потолка) — корпус не собирается лёжа и не поднимается собранным, а собирается в проектном положении у стены; выставление по уровню и крепление к стене выполняются по корпусу, собранному на месте.

| | | | | | |
|---|---|---|---|---|---|
| | | | | | Проект: Трёхкомнатная квартира |
| | Лист | № док. | Подпись | Дата | |
| Дизайнер | Кырлан А.С. | | | 05.10.26 | Шкафы. Монтажная схема |

| Стадия | Лист | Листов |
|---|---|---|
| П | 7 | 89 |

выпуск 05.10.2026 № 6a37468da7 · стр. 7 из 89

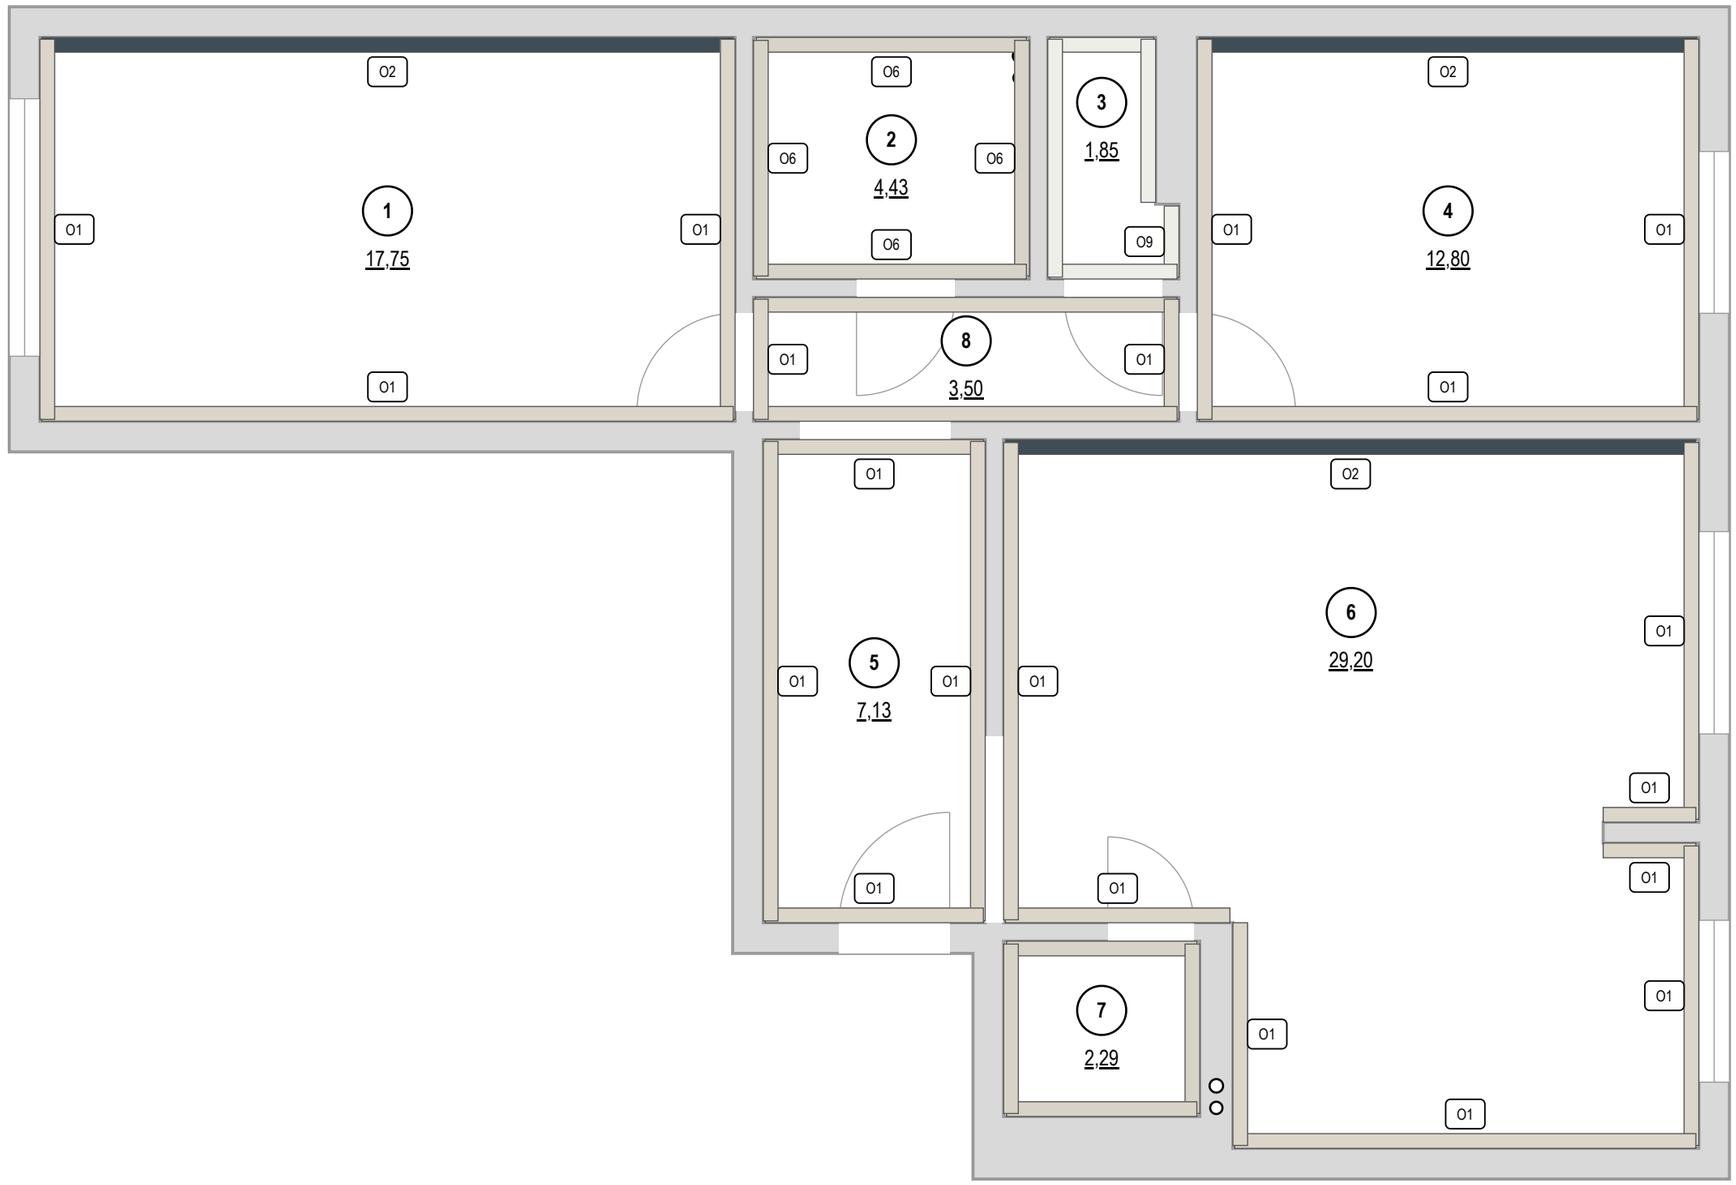


## Покрытия стен

| Марка | Покрытие | Помещение: S, м² | Итого, м² |
|---|---|---|---|
| O1 | окраска Farrow & Ball · No. 241 «Skimming Stone» | 1: 24,8; 4: 22,0; 5: 21,6; 6: 34,2; 8: 13,9 | 116,4 |
| O2 | окраска Farrow & Ball · No. 30 «Hague Blue» | 1: 14,1; 4: 10,2; 6: 14,1 | 38,3 |
| O6 | облицовка плиткой · 600×1200 мм | 2: 18,1; 7: 12,6 | 30,8 |
| O9 | окраска Tikkurila · V503 «Winter» | 3: 13,8 | 13,8 |

Площади — нетто, по развёрткам (за вычетом проёмов и фартука); высоты помещений — от чистого пола.

| | | | | | |
|---|---|---|---|---|---|
| | | | | | Проект: Трёхкомнатная квартира |
| | Лист | № док. | Подпись | Дата | |
| Дизайнер | Кырлан А.С. | | | 05.10.26 | Карта покрытий стен |
| | | | | | Стадия: П; Лист: 8; Листов: 89 |

## Колерная карта по помещениям

| Помещение | Поверхность | Образец | Поз. | Система и код цвета | Производитель, линейка / материал, артикул | Блеск | Класс EN 13300 | LRV | Площадь |
|---|---|---|---|---|---|---|---|---|---|
| **1. Спальня 1** 17,75 м² | стены | | **K1** | Farrow & Ball No. 241 | Farrow & Ball · Modern Emulsion | матовая | 1 | 67 | 25,0 м² |
| | акцент А | | **K2** | Farrow & Ball No. 30 | Farrow & Ball · Modern Emulsion | матовая | 1 | 7 | 14,2 м² |
| | потолок | | **K3** | Tikkurila V503 | Tikkurila · Anti-Reflex 2 | глубокомат. | 2 | 86 | 17,8 м² |
| | пол | | **KM1** | по образцу | инженерная доска · аналог по хар. | | | | 17,8 м² |
| | плинтус | | **K4** | Farrow & Ball No. 241 | МДФ · в цвет Farrow & Ball | | | 67 | 16,8 м |
| **2. Ванная** 4,43 м² | стены | | **KM2** | по образцу | плитка · аналог по хар. | | | | 18,6 м² |
| | потолок | | **K5** | Tikkurila V503 | Tikkurila · Luja 7 | матовая | 1 | 86 | 4,4 м² |
| | пол | | **KM3** | по образцу | керамогранит · аналог по хар. | | | | 4,4 м² |
| **3. Гардеробная** 1,85 м² | стены | | **K6** | Tikkurila V503 | Tikkurila · Harmony | матовая | 1 | 86 | 14,7 м² |
| | потолок | | **K3** | Tikkurila V503 | Tikkurila · Anti-Reflex 2 | глубокомат. | 2 | 86 | 1,9 м² |
| | пол | | **KM1** | по образцу | инженерная доска · аналог по хар. | | | | 1,9 м² |
| | плинтус | | **K7** | Tikkurila V503 | МДФ · в цвет Tikkurila | | | 86 | 5,3 м |
| **4. Спальня 2** 12,8 м² | стены | | **K1** | Farrow & Ball No. 241 | Farrow & Ball · Modern Emulsion | матовая | 1 | 67 | 22,2 м² |
| | акцент А | | **K2** | Farrow & Ball No. 30 | Farrow & Ball · Modern Emulsion | матовая | 1 | 7 | 10,2 м² |
| | потолок | | **K3** | Tikkurila V503 | Tikkurila · Anti-Reflex 2 | глубокомат. | 2 | 86 | 12,8 м² |
| | пол | | **KM1** | по образцу | инженерная доска · аналог по хар. | | | | 12,8 м² |
| | плинтус | | **K4** | Farrow & Ball No. 241 | МДФ · в цвет Farrow & Ball | | | 67 | 13,6 м |
| **5. Прихожая** 7,13 м² | стены | | **K1** | Farrow & Ball No. 241 | Farrow & Ball · Modern Emulsion | матовая | 1 | 67 | 21,9 м² |
| | потолок | | **K3** | Tikkurila V503 | Tikkurila · Anti-Reflex 2 | глубокомат. | 2 | 86 | 7,1 м² |
| | пол | | **KM4** | по образцу | керамогранит · аналог по хар. | | | | 7,1 м² |
| | плинтус | | **K4** | Farrow & Ball No. 241 | МДФ · в цвет Farrow & Ball | | | 67 | 7,8 м |
| **6. Кухня-гостиная** 29,2 м² | стены | | **K1** | Farrow & Ball No. 241 | Farrow & Ball · Modern Emulsion | матовая | 1 | 67 | 35,5 м² |
| | акцент А | | **K2** | Farrow & Ball No. 30 | Farrow & Ball · Modern Emulsion | матовая | 1 | 7 | 14,2 м² |
| | потолок | | **K3** | Tikkurila V503 | Tikkurila · Anti-Reflex 2 | глубокомат. | 2 | 86 | 29,2 м² |
| | пол | | **KM1** | по образцу | инженерная доска · аналог по хар. | | | | 29,2 м² |
| | плинтус | | **K4** | Farrow & Ball No. 241 | МДФ · в цвет Farrow & Ball | | | 67 | 22,2 м |
| | фартук | | **KM5** | по образцу | керамогранит · аналог по хар. | | | | 1,9 м² |
| **7. Санузел 2** 2,29 м² | стены | | **KM2** | по образцу | плитка · аналог по хар. | | | | 13,1 м² |
| | потолок | | **K5** | Tikkurila V503 | Tikkurila · Luja 7 | матовая | 1 | 86 | 2,3 м² |
| | пол | | **KM3** | по образцу | керамогранит · аналог по хар. | | | | 2,3 м² |
| **8. Коридор** 3,5 м² | стены | | **K1** | Farrow & Ball No. 241 | Farrow & Ball · Modern Emulsion | матовая | 1 | 67 | 14,2 м² |
| | потолок | | **K3** | Tikkurila V503 | Tikkurila · Anti-Reflex 2 | глубокомат. | 2 | 86 | 3,5 м² |
| | пол | | **KM1** | по образцу | инженерная доска · аналог по хар. | | | | 3,5 м² |
| | плинтус | | **K4** | Farrow & Ball No. 241 | МДФ · в цвет Farrow & Ball | | | 67 | 4,5 м |

## Перечень выкрасов на согласование

| № | Код | Бренд / веер | Пом. / стена | Подложка | Формат | Статус |
|---|---|---|---|---|---|---|
| 1 | No. 241 | Farrow & Ball | 1, 4, 5, 6, 8 | ГКЛ, загрунтованный под эту краску; МДФ, загрунтованный под эмаль | 600×1000; 300×600 | к выполнению |
| 2 | No. 30 | Farrow & Ball | 1 А, 4 А, 6 А | ГКЛ, загрунтованный под эту краску | 600×1000 | к выполнению |
| 3 | V503 | Tikkurila | 1, 2, 3, 4, 5, 6, 7, 8 | ГКЛ, загрунтованный под эту краску; МДФ, загрунтованный под эмаль | 600×1000; 300×600 | к выполнению |

## Примечания

1. Цвет утверждается только по выкрасу на объекте: формат от А3 до 1000×1000 мм на загрунтованном ГКЛ, в 2 слоя (как на стене), не на белой шпаклёвке; смотреть днём и при свете проекта своего помещения, рядом с образцами пола и фасадов. Подпись на обороте: код, бренд и веер, дата.
2. Колеровка машинная в колеровочном центре бренда; каждый код — за один проход, одной партией на весь объём. Колеровщику передаётся только система и код утверждённого веера; плашки и HEX на листе — ориентир, печать не является эталоном цвета.
3. Класс мокрого истирания — EN 13300 (ISO 11998); блеск — по ГОСТ 31975 (ISO 2813), геометрия 60°. LRV — пересчёт координаты L каталога производителя (Y = ((L*+16)/116)³); «≈» — расчёт по HEX, справочно.
4. Площади поверхностей — тем же способом и с теми же цифрами, что в ведомости отделки (способ счёта — в общих указаниях); объём краски к заказу, фасовка и материалы КМ — в спецификации отделочных материалов.
5. Перечень выкрасов составлен по кодам колерной карты; к основному тону стен добавить на выкрас 2 соседних тона того же веера (светлее и темнее), статус отмечать в графе «Статус» при согласовании.

## Схема квартиры: цвет стен и акценты (б/м)

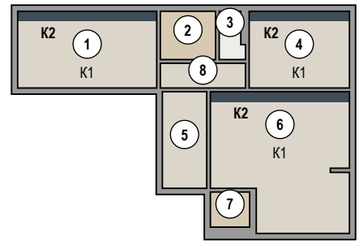


## Схема палитры проекта

Стиль: Современный (контемпорари) · схема: аналоговая

| основной | основной | второстепенный | акцентный |
|---|---|---|---|
| **Tikkurila V503** | **Farrow & Ball No. 241** | **Tikkurila H487** | **Farrow & Ball No. 30** |
| Winter<br>LRV 86<br>потолок 1,2,3,4,5,6,7,8; стены 3; плинтус 3; текстиль/декор 1,4,6 | Skimming Stone<br>LRV 67<br>стены 1,4,5,6,8; плинтус 1,4,5,6,8 | Pumice<br>LRV 57<br>текстиль/декор 1,4,6 | Hague Blue<br>LRV 7<br>акцент 1,4,6; текстиль/декор 1,4,6 |

План 60/30/10

| 60% | 30% | 10% |
|---|---|---|

Окраска, факт — по площади стен, акцентов, потолков

| 85% | 15% |
|---|---|

окрашено всего 251 м²; второстепенный тон несут мебель и текстиль

**Текстиль и декор в цветах вне палитры проекта**

- NCS S 3005-Y20R тёплый тауп-серый — пом. 1 (T3)
- Tikkurila V484 Driftwood — пом. 4 (T9), 6 (T15, T16, T19)
- Farrow & Ball No. 229 Elephant's Breath — пом. 4 (T10)
- Farrow & Ball No. 47 Green Smoke — пом. 4 (T11)

## Условные обозначения

- **K1** Farrow & Ball No. 241 · Skimming Stone · Modern Emulsion · матовая · кл. 1
- **K2** Farrow & Ball No. 30 · Hague Blue · Modern Emulsion · матовая · кл. 1
- **K3** Tikkurila V503 · Winter · Anti-Reflex 2 · глубокомат. · кл. 2
- **K4** Farrow & Ball No. 241 · Skimming Stone · МДФ
- **K5** Tikkurila V503 · Winter · Luja 7 · матовая · кл. 1
- **K6** Tikkurila V503 · Winter · Harmony · матовая · кл. 1
- **K7** Tikkurila V503 · Winter · МДФ
- дерево (доска, паркет, ламинат) — рисунок досок
- керамогранит, плитка, камень — сетка швов по формату
- **KM1** аналог: инженерная доска, дуб натуральный, масло, 1-полосная, 14/4 мм
- **KM2** плитка · аналог: керамогранит под травертин, матовый, 600×1200×9 мм
- **KM3** аналог: керамогранит ректифицированный под травертин, матовый, 600×600×9 мм
- **KM4** аналог: керамогранит ректифицированный под травертин, матовый, 600×1200×9 мм
- **KM5** аналог: керамогранит под травертин, матовый, 1200×600×9 мм

К — позиция окраски (код + продукт + блеск), КМ — позиция материала, тон КМ — по описанию артикула, эталон — образец материала; ≈ LRV — расчёт по HEX, справочно

| | | | | | |
|---|---|---|---|---|---|
| | | | | | Проект: Трёхкомнатная квартира |
| | Лист | № док. | Подпись | Дата | |
| Дизайнер | Кырлан А.С. | | | 05.10.26 | Колерная карта |

| Стадия | Лист | Листов |
|---|---|---|
| П | 9 | 89 |

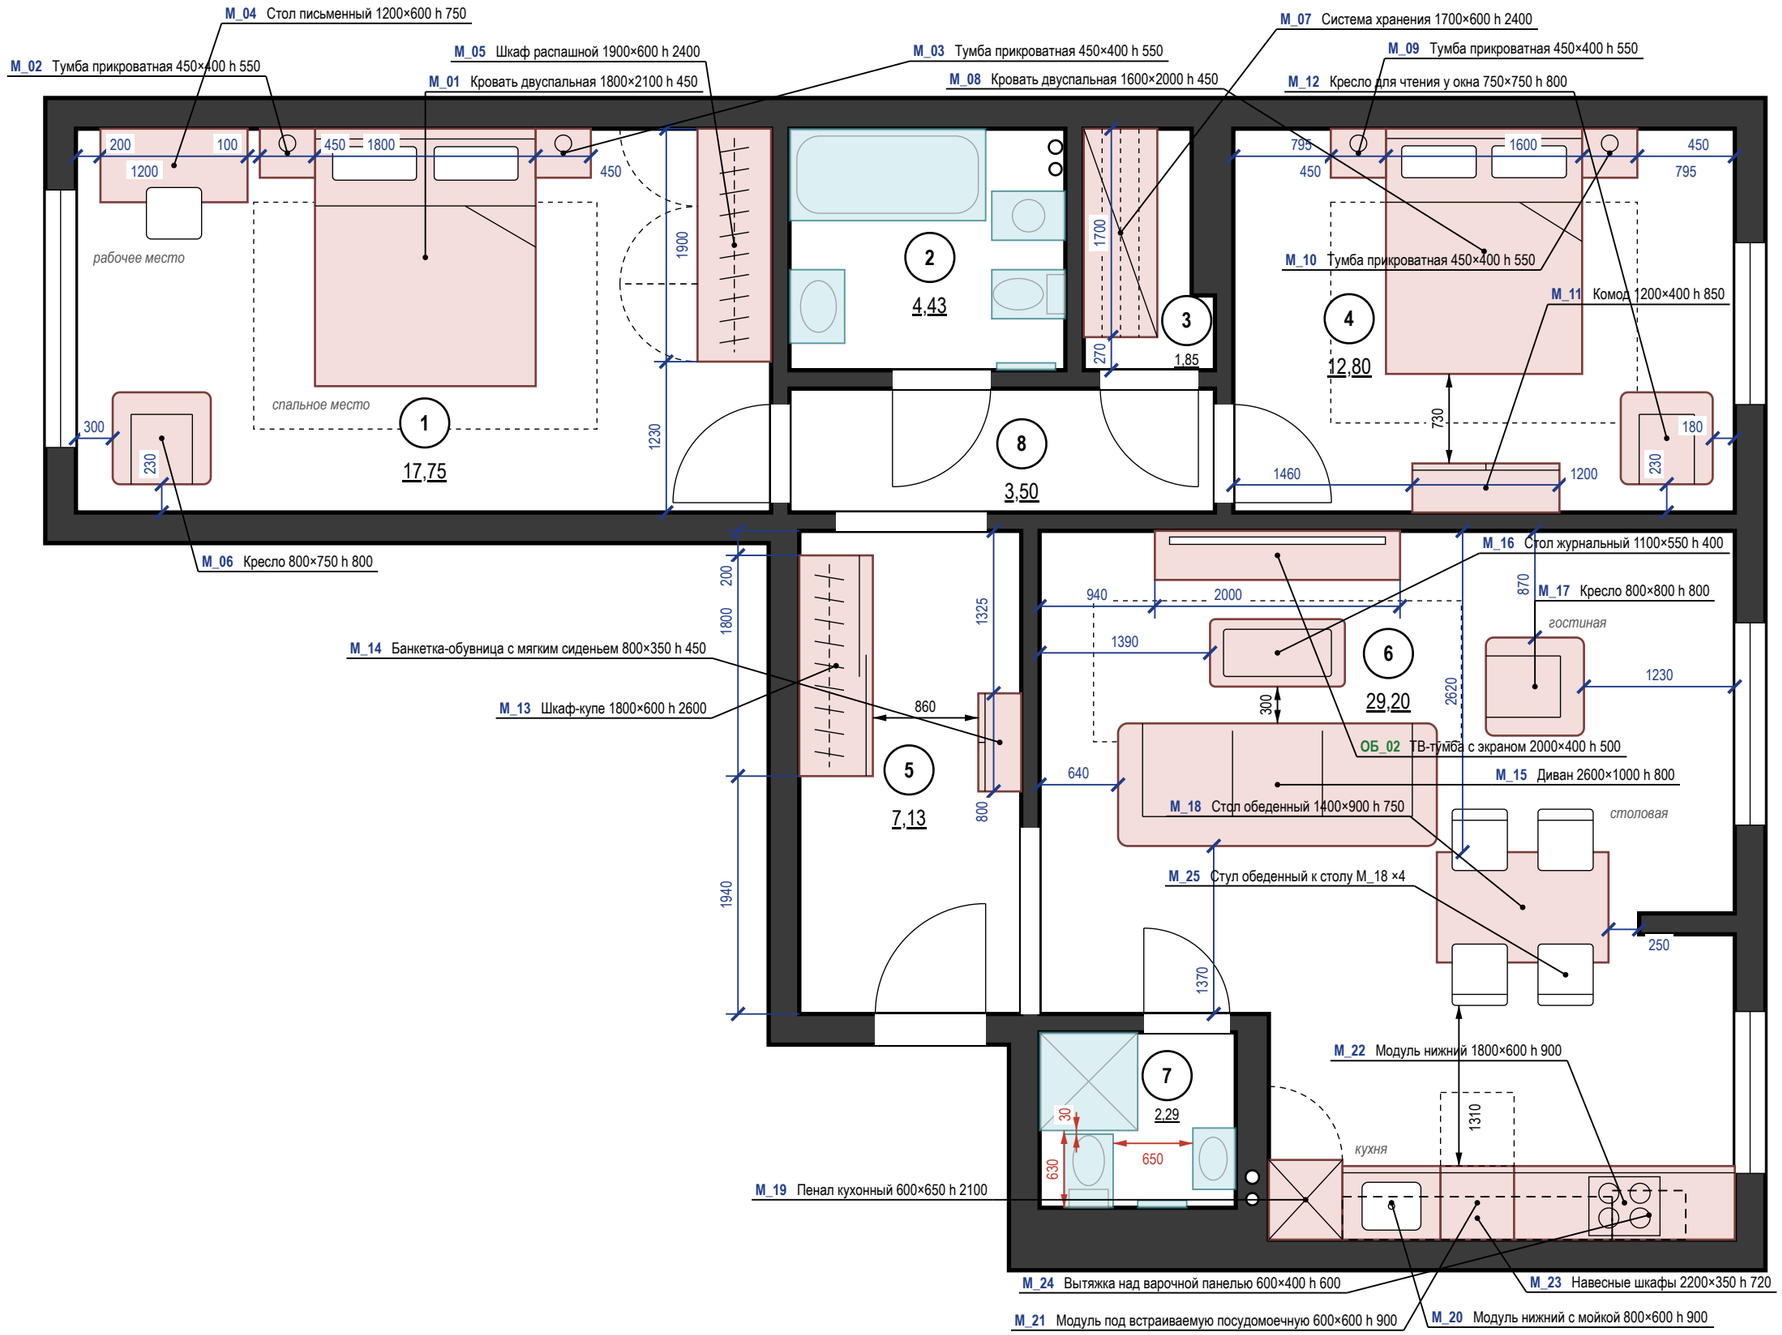


**Экспликация помещений**

лист обмерного плана · на плане — номера в марках

## Ведомость мебели и оборудования

| Марка | Наименование | Ш×Г×В, мм | Пом. | Кол. |
|---|---|---|---|---|
| M_01 | Кровать двуспальная | 1800×2100×450 | 1 | 1 |
| M_02 | Тумба прикроватная | 450×400×550 | 1 | 1 |
| M_03 | Тумба прикроватная | 450×400×550 | 1 | 1 |
| M_04 | Стол письменный | 1200×600×750 | 1 | 1 |
| M_05 | Шкаф распашной | 1900×600×2400 | 1 | 1 |
| M_06 | Кресло | 800×750×800 | 1 | 1 |
| M_07 | Система хранения | 1700×600×2400 | 3 | 1 |
| M_08 | Кровать двуспальная | 1600×2000×450 | 4 | 1 |
| M_09 | Тумба прикроватная | 450×400×550 | 4 | 1 |
| M_10 | Тумба прикроватная | 450×400×550 | 4 | 1 |
| M_11 | Комод | 1200×400×850 | 4 | 1 |
| M_12 | Кресло для чтения у окна | 750×750×800 | 4 | 1 |
| M_13 | Шкаф-купе | 1800×600×2600 | 5 | 1 |
| M_14 | Банкетка-обувница с мягким сиденьем | 800×350×450 | 5 | 1 |
| ОБ_02 | ТВ-тумба с экраном | 2000×400×500 | 6 | 1 |
| M_15 | Диван | 2600×1000×800 | 6 | 1 |
| M_16 | Стол журнальный | 1100×550×400 | 6 | 1 |
| M_17 | Кресло | 800×800×800 | 6 | 1 |
| M_18 | Стол обеденный | 1400×900×750 | 6 | 1 |
| M_19 | Пенал кухонный | 600×650×2100 | 6 | 1 |
| M_20 | Модуль нижний с мойкой | 800×600×900 | 6 | 1 |
| M_21 | Модуль под встраиваемую посудомоечную | 600×600×900 | 6 | 1 |
| M_22 | Модуль нижний | 1800×600×900 | 6 | 1 |
| M_23 | Навесные шкафы | 2200×350×720 | 6 | 1 |
| M_24 | Вытяжка над варочной панелью | 600×400×600 | 6 | 1 |
| M_25 | Стул обеденный к столу M_18 | 450×500×820 | 6 | 4 |

Ш — вдоль стены (изголовья), Г — от стены (длина кровати)

Материалы, модели, допуск замены — лист 11

## Примечания

1. Размеры — в мм от чистовых поверхностей стен; размеры мебели уточнить после отделочных работ; общие указания — лист 2.
2. Стулья обеденной группы (M_25 — 4 шт.) показаны в рабочем положении, задвинутыми под столешницу на 150 мм.

| | | | | | |
|---|---|---|---|---|---|
| | | | | | Проект: Трёхкомнатная квартира |
| | Лист | № док. | Подпись | Дата | |
| Дизайнер | Кырлан А.С. | | | 05.10.26 | План размещения мебели и оборудования |

| Стадия | Лист | Листов |
|---|---|---|
| П | 10 | 89 |

выпуск 05.10.2026 № 6a37468da7 · стр. 10 из 89

| Поз. | Наименование и техническая характеристика | Тип, марка, обозначение документа, опросного листа | Код продукции | Поставщик | Ед. измерения | Кол. | Масса 1 ед., кг | Примечание |
|---|---|---|---|---|---|---|---|---|
| | **Мебель встроенная и корпусная (изготовление по чертежам мебельщика)** | | | | | | | |
| M_05 | Шкаф распашной; корпус ЛДСП, фасады — матовая эмаль в цвет стен (Farrow & Ball No. 241); Ш×Г×В 1900×600×2400 мм | | | изготовление на заказ | шт. | 1 | | пом. 1; крепление к стене |
| M_07 | Система хранения: штанги, полки, ящики; каркас и полки — ЛДСП, декор «дуб натуральный»; Ш×Г×В 1700×600×2400 мм | | | изготовление на заказ | шт. | 1 | | пом. 3; крепление к стене |
| M_13 | Шкаф-купе; корпус ЛДСП, фасады — матовая эмаль в цвет стен (Farrow & Ball No. 241); Ш×Г×В 1800×600×2600 мм | | | изготовление на заказ | шт. | 1 | | пом. 5 |
| M_19 | Пенал кухонный, холодильник; корпус ЛДСП, фасады — матовая эмаль в тон стен; Ш×Г×В 600×650×2100 мм | | | изготовление на заказ | шт. | 1 | | пом. 6; крепление к стене |
| M_20 | Модуль нижний с мойкой; корпус ЛДСП, фасады — матовая эмаль в тон стен; Ш×Г×В 800×600×900 мм | | | изготовление на заказ | шт. | 1 | | пом. 6 |
| M_21 | Модуль под встраиваемую посудомоечную машину; корпус ЛДСП, фасады — матовая эмаль в тон стен; Ш×Г×В 600×600×900 мм | | | изготовление на заказ | шт. | 1 | | пом. 6 |
| M_22 | Модуль нижний: ящики, варочная панель, духовой шкаф, бутылочница; корпус ЛДСП, фасады — матовая эмаль в тон стен; Ш×Г×В 1800×600×900 мм | | | изготовление на заказ | шт. | 1 | | пом. 6 |
| M_23 | Навесные шкафы, 3 секции; корпус ЛДСП, фасады — матовая эмаль в тон стен; Ш×Г×В 2200×350×720 мм | | | изготовление на заказ | шт. | 1 | | пом. 6 |
| M_24 | Вытяжка над варочной панелью; корпус ЛДСП, фасады — матовая эмаль в тон стен; Ш×Г×В 600×400×600 мм | | | изготовление на заказ | шт. | 1 | | пом. 6 |
| | **Мебель покупная** | | | | | | | |
| M_01 | Кровать двуспальная; мягкое изголовье, обивка — ткань, цвет Tikkurila H487; Ш×Г×В 1800×2100×450 мм | | | аналог по характеристикам | шт. | 1 | | пом. 1; замена ≤ габарита |
| M_02, M_03, M_09, M_10 | Тумба прикроватная; шпон, дуб натуральный, матовое масло; Ш×Г×В 450×400×550 мм | | | аналог по характеристикам | шт. | 4 | | пом. 1, 4; замена ≤ габарита |
| M_04 | Стол письменный; шпон, дуб натуральный, матовое масло; Ш×Г×В 1200×600×750 мм | | | аналог по характеристикам | шт. | 1 | | пом. 1; замена ≤ габарита |
| M_06 | Кресло; обивка — ткань, цвет Tikkurila H487; Ш×Г×В 800×750×800 мм | | | аналог по характеристикам | шт. | 1 | | пом. 1; замена ≤ габарита |
| M_08 | Кровать двуспальная; мягкое изголовье, обивка — ткань, цвет Tikkurila H487; Ш×Г×В 1600×2000×450 мм | | | аналог по характеристикам | шт. | 1 | | пом. 4; замена ≤ габарита |
| M_11 | Комод; шпон, дуб натуральный, матовое масло; Ш×Г×В 1200×400×850 мм | | | аналог по характеристикам | шт. | 1 | | пом. 4; крепление к стене; замена ≤ габарита |
| M_12 | Кресло для чтения у окна; обивка — ткань, цвет Tikkurila H487; Ш×Г×В 750×750×800 мм | | | аналог по характеристикам | шт. | 1 | | пом. 4; замена ≤ габарита |
| M_14 | Банкетка-обувница с мягким сиденьем, над ней настенная вешалка с полкой (низ 1650); шпон, дуб натуральный, матовое масло; Ш×Г×В 800×350×450 мм | | | аналог по характеристикам | шт. | 1 | | пом. 5; замена ≤ габарита |
| M_15 | Диван; обивка — ткань, цвет Tikkurila H487; Ш×Г×В 2600×1000×800 мм | | | аналог по характеристикам | шт. | 1 | | пом. 6; замена ≤ габарита |
| M_16 | Стол журнальный; шпон, дуб натуральный, матовое масло; Ш×Г×В 1100×550×400 мм | | | аналог по характеристикам | шт. | 1 | | пом. 6; замена ≤ габарита |
| M_17 | Кресло; обивка — ткань, цвет Tikkurila H487; Ш×Г×В 800×800×800 мм | | | аналог по характеристикам | шт. | 1 | | пом. 6; замена ≤ габарита |
| M_18 | Стол обеденный; шпон, дуб натуральный, матовое масло; Ш×Г×В 1400×900×750 мм | | | аналог по характеристикам | шт. | 1 | | пом. 6; замена ≤ габарита |
| M_25 | Стул обеденный к столу M_18; обивка — ткань, цвет Tikkurila H487; каркас — дуб натуральный; Ш×Г×В 450×500×820 мм | | | аналог по характеристикам | шт. | 4 | | пом. 6; замена ≤ габарита |
| ОБ_02 | ТВ-тумба с экраном; шпон, дуб натуральный, матовое масло; Ш×Г×В 2000×400×500 мм | | | аналог по характеристикам | шт. | 1 | | пом. 6; замена ≤ габарита |
| | **Техника встраиваемая и бытовая, светильники под розетки** | | | | | | | |
| | Стиральная машина, место по листу ВК (ОБ_01); Ш×Г 600×400 мм | | | аналог по характеристикам | шт. | 1 | | пом. 2; по схеме изготовителя |
| | Холодильник встраиваемый, в модуле M_19 | | | аналог по характеристикам | шт. | 1 | | пом. 6; по схеме изготовителя |
| | Посудомоечная машина встраиваемая, в модуле M_21; ниша 600 мм | | | аналог по характеристикам | шт. | 1 | | пом. 6; по схеме изготовителя |
| | Варочная панель встраиваемая, электрическая, в модуле M_22 | | | аналог по характеристикам | шт. | 1 | | пом. 6; по схеме изготовителя |
| | Духовой шкаф встраиваемый, в модуле M_22 | | | аналог по характеристикам | шт. | 1 | | пом. 6; по схеме изготовителя |
| | Вытяжка, в модуле M_24 | | | аналог по характеристикам | шт. | 1 | | пом. 6; по схеме изготовителя |

## Примечания

1. Позиции мебели совпадают с марками на плане расстановки; размеры Ш×Г×В — Ш вдоль стены, Г от стены.
2. Встроенная и корпусная мебель изготавливается по чертежам мебельщика после контрольного обмера; графы «Тип, марка» и «Код продукции» для неё не заполняются (ГОСТ 21.110-2013).
3. Покупные изделия — аналог по характеристикам: заменять только на изделия не больше указанного габарита и того же материала и цвета.
4. Материал и цвет, не указанные в данных изделия, приняты по концепции: тон дерева — по полу, обивка — по вторичному цвету палитры; образцы согласовать до заказа.
5. Масса 1 ед. для изделий до 25 кг не указывается. Техника — по монтажным схемам изготовителя; выводы — по листам ЭОМ и ВК.

| | | | | | |
|---|---|---|---|---|---|
| | | | | | Проект: Трёхкомнатная квартира |
| | Лист | № док. | Подпись | Дата | |
| Дизайнер | Кырлан А.С. | | | 05.10.26 | Спецификация мебели и оборудования |

| Стадия | Лист | Листов |
|---|---|---|
| П | 11 | 89 |

| Поз. | Наименование и техническая характеристика | Тип, марка, обозначение документа, опросного листа | Код продукции | Поставщик | Ед. измерения | Кол. | Масса 1 ед., кг | Примечание |
|---|---|---|---|---|---|---|---|---|
| | Торшер, у поз. М_06; абажур — ткань или опаловое стекло; лампа 2700 K | | | аналог по характеристикам | шт. | 1 | | пом. 1; розетка Р5 (ЭОМ) |
| | Торшер, у поз. ОБ_02; абажур — ткань или опаловое стекло; лампа 2700 K | | | аналог по характеристикам | шт. | 1 | | пом. 6; розетка Р21 (ЭОМ) |
| | **Текстиль** | | | | | | | |
| Т1 | Портьеры-волна; лён 100 %; цвет Tikkurila H487; карниз 2500 мм, высота 2610 мм, сборка 2 | | | аналог по характеристикам | шт. | 2 | | пом. 1 |
| Т2 | Тюль; полиэстер 100 %; цвет Tikkurila V503; карниз 2500 мм, высота 2610 мм, сборка 2,5 | | | аналог по характеристикам | шт. | 1 | | пом. 1 |
| Т3 | Ковёр под кроватью; шерсть 80 %, хлопок 20 %; цвет NCS S 3005-Y20R; 2800×1850 мм | | | аналог по характеристикам | шт. | 1 | | пом. 1; с подложкой |
| Т4 | Подушки декоративные на кровать; лён 100 %; цвет Tikkurila H487 | | | аналог по характеристикам | шт. | 3 | | пом. 1 |
| Т5 | Подушки на кровать, акцент; хлопковый бархат 100 %; цвет Farrow & Ball No. 30 | | | аналог по характеристикам | шт. | 2 | | пом. 1 |
| Т6 | Плед на кровать; шерсть мериноса 100 %; цвет Farrow & Ball No. 30 | | | аналог по характеристикам | шт. | 1 | | пом. 1 |
| Т7 | Портьеры-волна; лён 100 %; цвет Tikkurila H487; карниз 1820 мм, высота 2610 мм, сборка 2 | | | аналог по характеристикам | шт. | 2 | | пом. 4 |
| Т8 | Тюль; полиэстер 100 %; цвет Tikkurila V503; карниз 1820 мм, высота 2610 мм, сборка 2,5 | | | аналог по характеристикам | шт. | 1 | | пом. 4 |
| Т9 | Ковёр под кроватью; шерсть 100 %; цвет Tikkurila V484; 2500×1800 мм | | | аналог по характеристикам | шт. | 1 | | пом. 4; с подложкой |
| Т10 | Подушки декоративные на кровать; букле (шерсть 60 %, полиэстер 40 %); цвет Farrow & Ball No. 229 | | | аналог по характеристикам | шт. | 3 | | пом. 4 |
| Т11 | Подушки на кровать, акцент; хлопковый бархат 100 %; цвет Farrow & Ball No. 47 | | | аналог по характеристикам | шт. | 2 | | пом. 4 |
| Т12 | Плед на кровать; шерсть мериноса 100 %; цвет Farrow & Ball No. 30 | | | аналог по характеристикам | шт. | 1 | | пом. 4 |
| Т13 | Портьеры-волна (гостиная); лён 70 %, вискоза 30 %; цвет Tikkurila H487; карниз 2250 мм, высота 2610 мм, сборка 2 | | | аналог по характеристикам | шт. | 2 | | пом. 6 |
| Т14 | Тюль (гостиная); полиэстер 100 %; цвет Tikkurila V503; карниз 2250 мм, высота 2610 мм, сборка 2,5 | | | аналог по характеристикам | шт. | 1 | | пом. 6 |
| Т15 | Римская штора (кухня); лён 100 %; цвет Tikkurila V484; карниз 1400 мм, высота 1620 мм | | | аналог по характеристикам | шт. | 1 | | пом. 6 |
| Т16 | Ковёр в зоне отдыха; шерсть 100 %; цвет Tikkurila V484; 3000×1150 мм | | | аналог по характеристикам | шт. | 1 | | пом. 6; с подложкой |
| Т17 | Подушки на диван; букле (шерсть 60 %, полиэстер 40 %); цвет Tikkurila H487 | | | аналог по характеристикам | шт. | 3 | | пом. 6 |
| Т18 | Подушки на диван, акцент; хлопковый бархат 100 %; цвет Farrow & Ball No. 30 | | | аналог по характеристикам | шт. | 2 | | пом. 6 |
| Т19 | Плед на диван; альпака 50 %, шерсть 50 %; цвет Tikkurila V484 | | | аналог по характеристикам | шт. | 1 | | пом. 6 |
| | **Декор** | | | | | | | |
| ДК1 | Картина над кроватью: абстракция, холст, тонкая рама из дуба; 1200×700 мм; низ на 1300 мм от пола | | | аналог по характеристикам | шт. | 1 | 4 | пом. 1; крепление к стене |
| ДК2 | Зеркало над умывальником, влагостойкое; 600×750 мм; низ на 1100 мм от пола | | | аналог по характеристикам | шт. | 1 | 4 | пом. 2; крепление к стене |
| ДК3 | Картина над кроватью: графика в паспарту, рама — дуб; 1000×700 мм; низ на 1300 мм от пола | | | аналог по характеристикам | шт. | 1 | 4 | пом. 4; крепление к стене |
| ДК4 | Зеркало в рост в тонкой чёрной раме; рама — чёрный матовый; 600×1600 мм; низ на 300 мм от пола | | | аналог по характеристикам | шт. | 1 | 12 | пом. 4; крепление: анкер для пустотелых оснований, 4 шт. |
| ДК5 | Зеркало; рама — чёрный матовый; 800×1800 мм; низ на 550 мм от пола | | | аналог по характеристикам | шт. | 1 | 18 | пом. 5; крепление: анкер, 4 шт. |
| ДК6 | Картина: крупная абстракция в тёплой гамме, холст на подрамнике; 1200×900 мм; центр на 1550 мм от пола | | | аналог по характеристикам | шт. | 1 | 6 | пом. 6; крепление: анкер, 2 шт. |
| ДК7 | Растение в кашпо; 450×450 мм | | | аналог по характеристикам | шт. | 1 | | пом. 6 |
| ДК8 | Ваза керамическая с ветками на обеденном столе; 200×350 мм; на М_18 | | | аналог по характеристикам | шт. | 1 | | пом. 6 |
| ДК9 | Зеркало над умывальником, влагостойкое; 500×700 мм; низ на 1100 мм от пола | | | аналог по характеристикам | шт. | 1 | 4 | пом. 7; крепление к стене |

| | | | | | | | | |
|---|---|---|---|---|---|---|---|---|
| | | | | | | Проект: Трёхкомнатная квартира | | |
| | Лист | № док. | Подпись | Дата | | | | |
| Дизайнер | Кырлан А.С. | | | 05.10.26 | Спецификация мебели и оборудования (продолжение) | Стадия | Лист | Листов |
| | | | | | | П | 12 | 89 |

выпуск 05.10.2026 № 6a37468da7 · стр. 12 из 89

## Ведомость изделий

| Марка | Наименование | Пом. | Ш×Г×В, мм | Корпус | Фасад | Кромка, мм скр./вид. | Кол. |
|---|---|---|---|---|---|---|---|
| M_05 | Шкаф распашной | 1 | 1900×600×2400 | ЛДСП 16 | МДФ 18, эмаль матовая | 0,4 / 2 | 1 |
| M_07 | Система хранения | 3 | 1700×600×2400 | ЛДСП 16 | без фасадов; ящики — МДФ 18, эмаль матовая | 0,4 / 2 | 1 |
| M_13 | Шкаф-купе | 5 | 1800×600×2600 | ЛДСП 16 | рифлёные панели МДФ в алюминиевом профиле | 0,4 / 2 | 1 |
| M_22 | Модуль нижний: карго, духовой шкаф, ящики, варочная | 6 | 1800×600×900 | ЛДСП 16 | МДФ 18, эмаль матовая | 0,4 / 2 | 1 |
| M_24 | Модуль навесной: полки | 6 | 600×400×600 | ЛДСП 16 | МДФ 18, эмаль матовая | 0,4 / 2 | 1 |
| M_23 | Модуль навесной: полки, сушка | 6 | 2200×350×720 | ЛДСП 16 | МДФ 18, эмаль матовая | 0,4 / 2 | 1 |
| M_21 | Модуль нижний: ПММ | 6 | 600×600×900 | ЛДСП 16 | МДФ 18, эмаль матовая | 0,4 / 2 | 1 |
| M_20 | Модуль нижний: мойка | 6 | 800×600×900 | ЛДСП 16 | МДФ 18, эмаль матовая | 0,4 / 2 | 1 |
| M_19 | Пенал: холодильник встр. | 6 | 600×650×2100 | ЛДСП 16 | МДФ 18, эмаль матовая | 0,4 / 2 | 1 |

## Ведомость встраиваемой техники

| Поз. | Прибор | Ниша, вырез, мм | Вентиляция | Питание | Схема |
|---|---|---|---|---|---|
| M_22.2 | Духовой шкаф встраиваемый, 60 см | ниша 560 × 595, глубина ≥ 550 | зазор за шкафом, вырез в задней стенке | вывод кабеля под шкафом | по модели |
| M_22.2 | Варочная панель индукционная, 60 см | вырез в столешнице 560 × 490 | | вывод кабеля под модулем | по модели |
| M_21 | Посудомоечная машина встраиваемая, 60 см | ниша 600 × 862 (от пола до низа столешницы) | зазор в цоколе, по схеме | розетка в соседнем модуле | по модели |
| M_20 | Мойка врезная / подстольная с сифоном | вырез по шаблону, ориентир 700 × 480 | | смеситель — выводы ВК | по модели |
| M_19 | Холодильник встраиваемый, ниша 1780 | ниша 1780 × 560 × 550 | решётка в цоколе, канал за корпусом, выход сверху | розетка над нишей или в соседнем модуле | по модели |
| M_22.2 | Вытяжка настенная, 60 см | низ ≥ 650 над панелью | воздуховод к вентканалу, короб до потолка | вывод кабеля в коробе | по модели |

## Ведомость фурнитуры

| № | Фурнитура | Тип, размер | Изделия | Кол. |
|---|---|---|---|---|
| 1 | Петля накладная 110° с доводчиком | чашка 35 мм | M_05, M_24, M_23, M_20, M_19 | 51 |
| 2 | Полкодержатель с фиксацией | ø5 мм | M_05, M_07, M_13, M_24, M_23, M_19 | 96 |
| 3 | Штанга овальная 30×15, L = 926 | + 2 держателя | M_05 | 1 |
| 4 | Опора регулируемая с цоколем на клипсах | ход 20 мм | M_05, M_07, M_13 | 24 |
| 5 | Анкер по основанию стены | по таблице крепежа | M_05, M_07, M_13, M_24, M_23 | 28 |
| 6 | Уголок крепления к стене от опрокидывания | стальной | M_05, M_07, M_13, M_19 | 8 |
| 7 | Штанга овальная 30×15, L = 545 | + 2 держателя | M_07 | 3 |
| 8 | Система дверей купе: профиль, направляющие, ролики | на 2 двери | M_13 | 1 |
| 9 | Ручка-профиль вертикальная | в цвет профиля | M_13 | 2 |
| 10 | Штанга овальная 30×15, L = 876 | + 2 держателя | M_13 | 1 |
| 11 | Полка для обуви выдвижная наклонная | ширина 876 | M_13 | 3 |
| 12 | Карго выдвижное 3-уровневое | ширина 350 | M_22 | 1 |
| 13 | Направляющие полного выдвижения с доводчиком NL 500 | пара | M_22 | 4 |
| 14 | Ручка-профиль | латунь матовая | M_22, M_24, M_23, M_21, M_20, M_19 | 19 |
| 15 | Опора кухонная регулируемая 100–120 мм | + клипса цоколя | M_22, M_21, M_20, M_19 | 20 |
| 16 | Навес регулируемый для навесного шкафа | пара на секцию | M_24, M_23 | 4 |
| 17 | Шина монтажная | L = 540 | M_24 | 1 |
| 18 | Сушка для посуды в шкаф | ширина 800 | M_23 | 1 |
| 19 | Шина монтажная | L = 2140 | M_23 | 1 |
| 20 | Комплект навески фасада ПММ | из поставки машины | M_21 | 1 |

## Примечания

1. Модели техники выбирает заказчик до изготовления мебели; ниши, вырезы и вентиляция — по монтажной схеме выбранной модели (условие гарантии), её номер вносится в ведомость.
2. Количество фурнитуры — по чертежам изделий; запас крепежа 5 %. Аналоги — по характеристикам (доводчик, нагрузка, ход).
3. Цвет корпусов, фасадов и профилей — по колерной карте проекта.

| | | | | | |
|---|---|---|---|---|---|
| | | | | | Проект: Трёхкомнатная квартира |
| | Лист | № док. | Подпись | Дата | Ведомости изделий, техники и фурнитуры |
| Дизайнер | Кырлан А.С. | | | 05.10.26 | |

| Стадия | Лист | Листов |
|---|---|---|
| П | 13 | 89 |

выпуск 05.10.2026 № 6a37468da7 · стр. 13 из 89

## Фрагмент 1. Ванная (пом. 2)

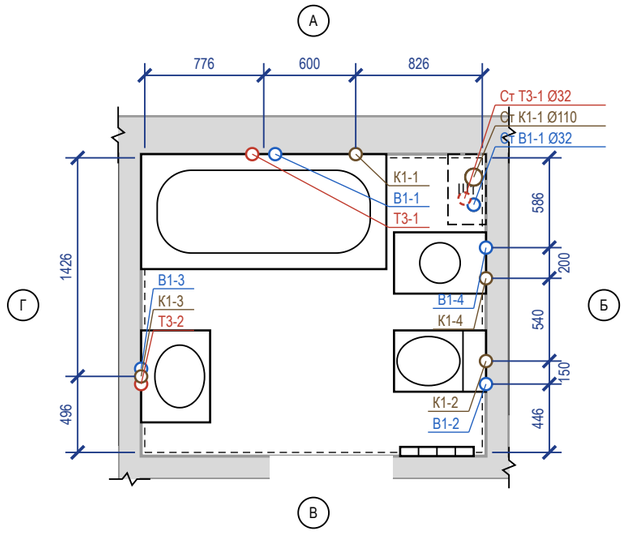


## Фрагмент 2. Кухня-гостиная (пом. 6)

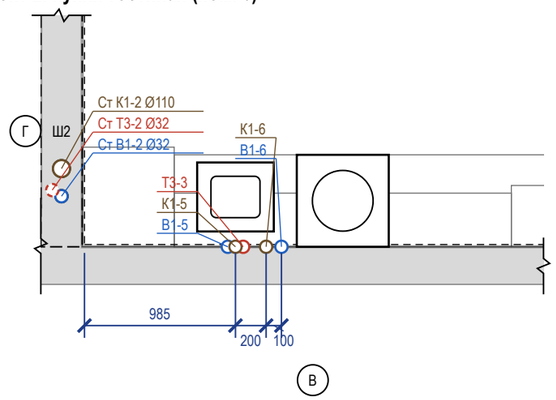


## Фрагмент 3. Санузел 2 (пом. 7)

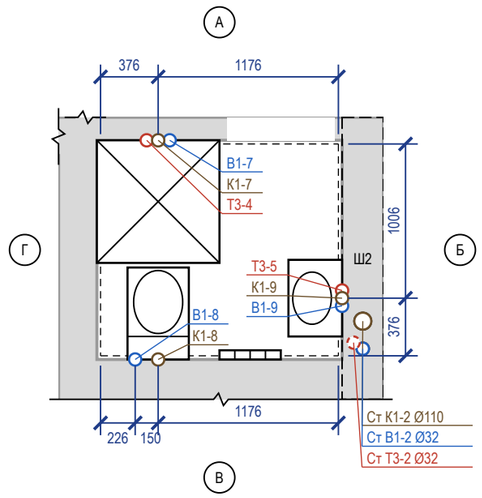


## Ведомость привязок выводов

| Код | Прибор | Ø | H, мм | Привязка от чист. стен, мм | Прим. |
|---|---|---|---|---|---|
| В1-1 | С_01 ванна | ½" | 800 | ст. А: 851 от Г | межос. 150 |
| Т3-1 | С_01 ванна | ½" | 800 | ст. А: 701 от Г | межос. 150 |
| К1-1 | С_01 ванна | Ø50 | 50 | ст. А: 826 от Б | |
| В1-2 | С_02 унитаз подвесной | ½" | 250 | ст. Б: 446 от В | в раме инсталляции |
| К1-2 | С_02 унитаз подвесной | Ø110 | 220 | ст. Б: 596 от В | |
| В1-3 | С_03 умывальник | ½" | 600 | ст. Г: 546 от В | межос. 100 |
| Т3-2 | С_03 умывальник | ½" | 600 | ст. Г: 446 от В | межос. 100 |
| К1-3 | С_03 умывальник | Ø50 | 500 | ст. Г: 496 от В | |
| В1-4 | ОБ_01 стиральная машина | ½" | 600 | ст. Б: 586 от А | кран машины |
| К1-4 | ОБ_01 стиральная машина | Ø50 | 600 | ст. Б: 786 от А | |
| В1-5 | С_05 мойка кухонная | ½" | 600 | ст. В: 935 от Г | межос. 100 |
| Т3-3 | С_05 мойка кухонная | ½" | 600 | ст. В: 1035 от Г | межос. 100 |
| К1-5 | С_05 мойка кухонная | Ø50 | 400 | ст. В: 985 от Г | |
| В1-6 | ОБ_03 посудомоечная машина | ½" | 550 | ст. В: 1285 от Г | кран ПММ в шкафу мойки |
| К1-6 | ОБ_03 посудомоечная машина | Ø40 | 550 | ст. В: 1185 от Г | слив ПММ в шкафу мойки |
| В1-7 | С_06 душ | ½" | 1200 | ст. А: 451 от Г | межос. 150 |
| Т3-4 | С_06 душ | ½" | 1200 | ст. А: 301 от Г | межос. 150 |
| К1-7 | С_06 душ | Ø50 | 70 | ст. А: 376 от Г | сифон поддона |
| В1-8 | С_07 унитаз подвесной | ½" | 250 | ст. В: 226 от Г | в раме инсталляции |
| К1-8 | С_07 унитаз подвесной | Ø110 | 220 | ст. В: 376 от Г | |
| В1-9 | С_08 умывальник | ½" | 600 | ст. Б: 326 от В | межос. 100 |
| Т3-5 | С_08 умывальник | ½" | 600 | ст. Б: 426 от В | межос. 100 |
| К1-9 | С_08 умывальник | Ø50 | 500 | ст. Б: 376 от В | |

## Условные обозначения

- вывод В1 (код — в ведомости привязок)
- вывод Т3 (код — в ведомости привязок)
- вывод К1 (код — в ведомости привязок)
- сантехприбор по расстановке (габарит модели)
- чистовая поверхность стены (от неё привязки)
- стояк «Ст К1-N / Ст В1-N» (ГОСТ 21.601), Ø мм
- стояк Т3 не на обмере — принят в шахте рядом со Ст В1, сверить
- шахта / короб стояков, люк 300×400
- линия обрыва (граница фрагмента)
- А — обозначение стены А–Г (как на развёртках)

## Примечания

1. Привязки выводов даны от чистовых поверхностей стен (облицовка на сторону: ванная — 24 мм (штукатурка 10 + клей 5 + плитка 9); кухня-гостиная — 24 мм (фартук: штукатурка 10 + клей 5 + плитка 9); санузел 2 — 24 мм (штукатурка 10 + клей 5 + плитка 9)); эти же грани — на развёртках и в раскладке плитки. Высоты — от чистого пола помещения.
2. До черновой разводки сверить по паспорту выбранного прибора (смеситель, инсталляция, сифон).
3. Горячая вода (Т3) — слева от холодной (В1), если смотреть на прибор. Допуск установки выводов: ±5 мм в группе, ±20 мм у отдельно стоящих.
4. Расчёт систем водоснабжения и канализации и подбор оборудования выполняет проектная организация; лист задаёт места и высоты выводов.
5. Посудомоечная машина ОБ_03: кран и слив — отдельными выводами в шкафу мойки (не за машиной), до машины ≤ 1500 мм.
6. Ст Т3-1, Ст Т3-2 на обмере не показаны: приняты рядом с Ст В1-1, Ст В1-2 (в МКД стоят группой); положение сверить на объекте до разметки.
7. Стояки в коробах/шахтах Ш1, Ш2 не замоноличивать; стояк К1 в коробе — звукоизоляция стояка в коробе без жёсткого контакта с трубой; к арматуре и ревизиям — люк не меньше 300×400.

| | | | | | |
|---|---|---|---|---|---|
| | | | | | Проект: Трёхкомнатная квартира |
| | Лист | № док. | Подпись | Дата | |
| Дизайнер | Кырлан А.С. | | | 05.10.26 | План выводов сантехники |
| | | | | | Стадия: П; Лист: 14; Листов: 89 |

выпуск 05.10.2026 № 6a37468da7 · стр. 14 из 89

## План квартиры (М 1:200)

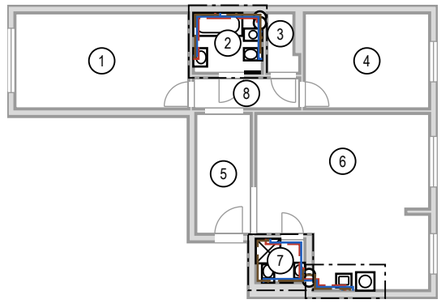


## Фр. 2. Кухня-гостиная (М 1:25)

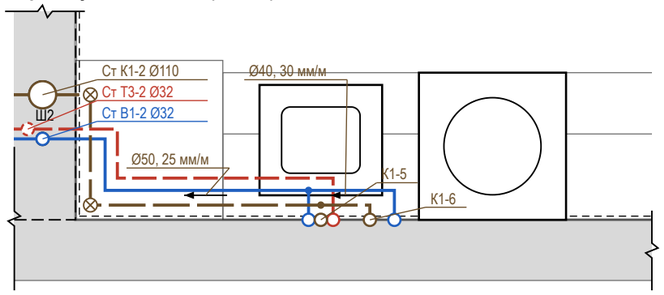


## Фр. 1. Ванная (М 1:25)

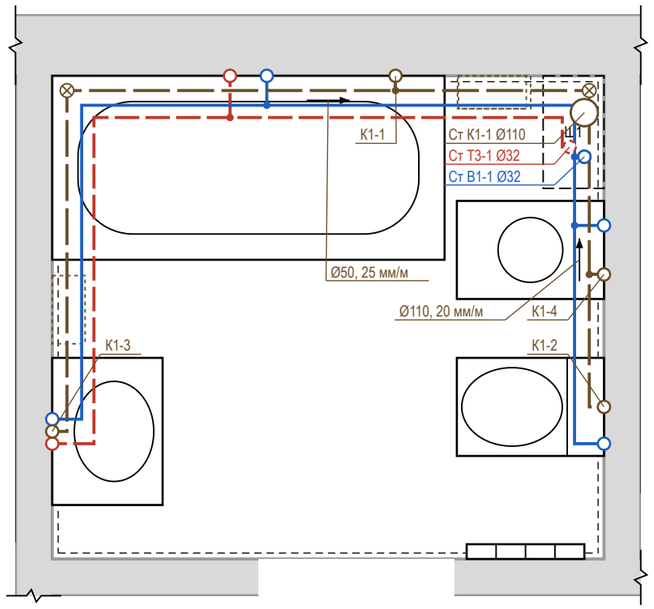


## Фр. 3. Санузел 2 (М 1:25)

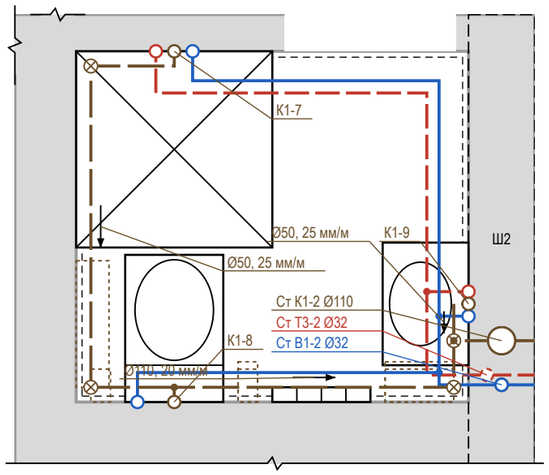


## Условные обозначения

- В1 — водопровод хозяйственно-питьевой (ХВС), PP-R Ø20
- Т3 — горячее водоснабжение, подача (ГВС), PP-R Ø20
- К1 — канализация бытовая
- направление уклона К1 / пола: Ø, мм на 1 м
- ревизия (прочистка) К1 — доступ сохранить
- тройник (ответвление к прибору)
- короб К1 над чистым полом (ГКЛВ под плитку)
- вывод В1 (код — в ведомости привязок)
- вывод Т3 (код — в ведомости привязок)
- вывод К1 (код — в ведомости привязок)
- сантехприбор по расстановке (габарит модели)
- стояк «Ст К1-N / Ст В1-N» (ГОСТ 21.601), Ø мм
- стояк Т3 не на обмере — принят в шахте рядом со Ст В1, сверить
- шахта / короб стояков, люк 300×400
- линия обрыва (граница фрагмента)
- граница фрагмента на плане (Фр. N)

## Профиль выпусков К1 (до врезки в стояк)

| Выпуск | Прибор | Ø | L, м | i, мм/м | Δh, мм | Прокладка, мм |
|---|---|---|---|---|---|---|
| К1-8 | С_07 унитаз подвесной | Ø110 | 1,58 | 20 | 32 | короб 180×140 |
| К1-2 | С_02 унитаз подвесной | Ø110 | 1,28 | 20 | 26 | над полом за приборами |
| К1-3 | С_03 умывальник | Ø50 | 3,69 | 25 | 92 | короб 180×110 |
| К1-7 | С_06 душ | Ø50 | 3,58 | 25 | 89 | короб 170×110 |
| К1-5 | С_05 мойка кухонная | Ø50 | 1,65 | 25 | 41 | над полом за приборами |
| К1-1 | С_01 ванна | Ø50 | 0,96 | 25 | 24 | короб 110×110 |
| К1-4 | ОБ_01 стиральная машина | Ø50 | 0,74 | 25 | 19 | над полом за приборами |
| К1-9 | С_08 умывальник | Ø50 | 0,41 | 25 | 10 | над полом за приборами |
| К1-6 | ОБ_03 посудомоечная машина | Ø40 | 1,84 | 30 | 55 | над полом за приборами |

Короб h×b: h — от чистого пола, b — от чистовой стены. Стяжка 35 мм — лист полов.

## Узел ввода В1, Т3 (схема, без масштаба)

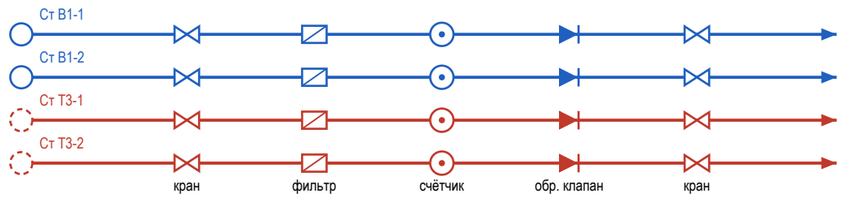


⊗ Ст К1-1, Ст К1-2: ревизия на стояке — люк в коробе

## Примечания

1. Трассы принципиальные, построены от стояков вдоль стен помещений; фактическое положение фиксируется исполнительной схемой с привязками (фото с рулеткой) до закрытия.
2. Уклон К1 не менее 1/d и не более 150 мм/м (СП 30.13330.2020, п. 19.1), приняты практические уклоны; поворот — двумя отводами 45°, ревизия после поворота, доступ сохранить. Стояк К1 в коробе — звукоизоляция стояка в коробе, без жёсткого контакта короба с трубой.
3. Решение по К1: стяжка 35 мм не укрывает трубы (нужно Ø + Δh + 45 мм) — выпуски идут над чистым полом вдоль стен: К1-2, К1-5, К1-4, К1-9, К1-6 — за приборами и в раме инсталляции; К1-8, К1-3, К1-7, К1-1 — в коробе ГКЛВ под плитку (размеры в профиле). Короба — на развёртках; отметку низа врезки в стояк замерить до черновых работ.
4. На каждом вводе В1 и Т3 — кран шаровой, фильтр, счётчик, обратный клапан; доступ через люк не меньше 300×400. Водопровод — в штробе стен или в коробах; трубы испытать давлением до закрытия (акт скрытых работ).
5. Расчёт систем, диаметры магистралей и подбор оборудования выполняет проектная организация; врезка и перенос стояков — по согласованию с управляющей организацией. Арматуру и привязки сверить по паспортам приборов.
6. Ст Т3-1, Ст Т3-2 на обмере не показаны: приняты рядом с Ст В1-1, Ст В1-2; положение сверить на объекте до разводки.

| | | | | | |
|---|---|---|---|---|---|
| | | | | | Проект: Трёхкомнатная квартира |
| | Лист | № док. | Подпись | Дата | |
| Дизайнер | Кырлан А.С. | | | 05.10.26 | Схема разводки водопровода и канализации |

| Стадия | Лист | Листов |
|---|---|---|
| П | 15 | 89 |

выпуск 05.10.2026 № 6a37468da7 · стр. 15 из 89

| Поз. | Наименование и техническая характеристика | Тип, марка, обозначение документа | Код продукции | Поставщик | Ед. изм. | Кол. | Масса 1 ед., кг | Примечание |
|---|---|---|---|---|---|---|---|---|
| | Санитарные приборы | | | | | | | |
| 1 | Ванна акриловая 1600×750 мм, с каркасом, экраном и отверстием слив-перелив | аналог | | выбор заказчика | шт | 1 | | С_01 |
| 2 | Унитаз подвесной безободковый, с сиденьем микролифт, крепёж и звукоизолирующая прокладка | аналог | | выбор заказчика | шт | 2 | | С_02, С_07 |
| 3 | Инсталляция для подвесного унитаза: рама высотой 1120 мм, бачок, клавиша смыва (ось клавиши 1050 мм от чистого пола) | аналог | | выбор заказчика | шт | 2 | | С_02, С_07; короб ГКЛВ |
| 4 | Умывальник подвесной 450×600 мм, с отверстием под смеситель и переливом | аналог | | выбор заказчика | шт | 1 | | С_03 |
| 5 | Умывальник подвесной 350×500 мм, с отверстием под смеситель и переливом | аналог | | выбор заказчика | шт | 1 | | С_08 |
| 6 | Поддон душевой низкий 800×800 мм, с сифоном и выпуском Ø50, на ножках/подиуме | аналог | | выбор заказчика | шт | 1 | | С_06 |
| 7 | Мойка кухонная врезная 500×450 мм, с переливом | аналог | | с кухонной мебелью | шт | 1 | | С_05 |
| 8 | Полотенцесушитель электрический, IP44, с терморегулятором | аналог | | выбор заказчика | шт | 2 | | С_04, С_09 |
| | Смесители, сифоны и арматура приборов | | | | | | | |
| 9 | Смеситель для ванны настенный однорычажный, межосевое 150 мм, с душевым набором (лейка, шланг, держатель) | аналог | | выбор заказчика | шт | 1 | | С_01 |
| 10 | Смеситель для умывальника однорычажный, с донным клапаном | аналог | | выбор заказчика | шт | 2 | | С_03, С_08 |
| 11 | Душевая система скрытого монтажа с термостатом: встраиваемая часть, верхний душ, ручная лейка | аналог | | выбор заказчика | шт | 1 | | С_06; встраиваемая часть — до плитки |
| 12 | Смеситель кухонный однорычажный, высокий излив | аналог | | выбор заказчика | шт | 1 | | С_05 |
| 13 | Обвязка ванны слив-перелив Ø40/50 с сифоном | аналог | | выбор заказчика | шт | 1 | | С_01 |
| 14 | Сифон для умывальника бутылочный Ø32/40–50, с гофрой к выпуску | аналог | | выбор заказчика | шт | 2 | | С_03, С_08 |
| 15 | Сифон для мойки с отводом для ПММ Ø40/50 | аналог | | выбор заказчика | шт | 1 | | С_05 |
| 16 | Сифон для стиральной машины встраиваемый в стену Ø50, с обратным клапаном | аналог | | выбор заказчика | шт | 1 | | ОБ_01 |
| 17 | Кран угловой ½"×½" с гибкой подводкой 40 см (умывальники, мойка) | аналог | | выбор заказчика | шт | 6 | | по 2 на прибор |
| 18 | Кран шаровой угловой ½"×¾" для подключения стиральной и посудомоечной машины | аналог | | выбор заказчика | шт | 2 | | ОБ_01, ОБ_03 |
| | Трубопроводы | | | | | | | |
| 19 | Труба полипропиленовая PP-R PN20 Ø20×3,4 (В1) | ГОСТ 32415-2013 | | выбор заказчика | м | 18,5 | 0,17 | 11,2 + 5,5 + 10 % |
| 20 | Труба PP-R, армированная стекловолокном, PN20 Ø20×2,8 (Т3) | ГОСТ 32415-2013 | | выбор заказчика | м | 13,5 | 0,15 | 8,2 + 3,8 + 10 % |
| 21 | Труба канализационная ПП Ø40 (К1) | ГОСТ 32414-2013 | | выбор заказчика | м | 1 | | 0,3 + 0,6 + 10 % |
| 22 | Труба канализационная ПП Ø50 (К1) | ГОСТ 32414-2013 | | выбор заказчика | м | 11 | | 7,7 + 2,1 + 10 % |
| 23 | Труба канализационная ПП Ø110 (К1) | ГОСТ 32414-2013 | | выбор заказчика | м | 4 | | 2,9 + 0,4 + 10 % |
| | Фасонные части и выводы | | | | | | | |
| 24 | Отвод канализационный ПП 45° Ø40 | ГОСТ 32414-2013 | | выбор заказчика | шт | 2 | | 2 шт. на поворот |
| 25 | Отвод канализационный ПП 45° Ø50 | ГОСТ 32414-2013 | | выбор заказчика | шт | 20 | | 2 шт. на поворот |
| 26 | Отвод канализационный ПП 45° Ø110 | ГОСТ 32414-2013 | | выбор заказчика | шт | 10 | | 2 шт. на поворот |
| 27 | Тройник канализационный ПП 45° (врезки ветвей) | ГОСТ 32414-2013 | | выбор заказчика | шт | 8 | | |
| 28 | Ревизия канализационная ПП (после поворота трассы) | ГОСТ 32414-2013 | | выбор заказчика | шт | 9 | | доступ сохранить |
| 29 | Фитинги PP-R Ø20: тройники, угольники 90° (ветви и повороты В1, Т3) | ГОСТ 32415-2013 | | выбор заказчика | шт | 34 | | |
| 30 | Водорозетка PP-R Ø20×½" настенная, с креплением | ГОСТ 32415-2013 | | выбор заказчика | шт | 14 | | коды — лист выводов |

| Поз. | Наименование и техническая характеристика | Тип, марка, обозначение документа | Код продукции | Поставщик | Ед. изм. | Кол. | Масса 1 ед., кг | Примечание |
|---|---|---|---|---|---|---|---|---|
| | Узлы ввода, люки, короба | | | | | | | |
| 31 | Кран шаровой латунный Ду15 PN16 (отключение ввода) | аналог | | выбор заказчика | шт | 4 | | Ст В1-1, Ст В1-2, Ст Т3-1, Ст Т3-2 |
| 32 | Фильтр сетчатый косой Ду15 | аналог | | выбор заказчика | шт | 4 | | |
| 33 | Счётчик воды крыльчатый Ду15 (ХВ, ГВ), с поверкой | аналог | | выбор заказчика | шт | 4 | | пломба УК |
| 34 | Клапан обратный Ду15 | аналог | | выбор заказчика | шт | 4 | | |
| 35 | Люк ревизионный нажимной под плитку 300×400 мм | аналог | | выбор заказчика | шт | 2 | | к стоякам и арматуре |
| 36 | Звукоизоляция стояка К1 в коробе: рулонный звукоизоляционный материал ≥ 10 мм, обмотка стояка на высоту этажа | аналог | | выбор заказчика | м | 5,4 | | Ст К1-1, Ст К1-2 |
| 37 | Короб К1 над полом: профиль ПН/ПС, ГКЛВ 12,5 мм под плитку | аналог | | выбор заказчика | м | 2,4 | | сечение — лист разводки |

## Примечания

1. Форма 1 ГОСТ 21.110-2013, ширины граф изменены по п. 4.1. «Аналог» — аналог по характеристикам: модели внести до черновых работ, привязки выводов сверить по паспортам.
2. Бытовая техника не входит (показана арматура подключения), мойка — в комплекте кухни. Длины труб — трасса листа разводки + подъёмы + 10 %.
3. Стояк К1 в коробе — звукоизоляция стояка в коробе без жёсткого контакта короба с трубой.
4. Расчёт систем водоснабжения и канализации, диаметры магистралей и подбор оборудования выполняет проектная организация.

| | | | | | Проект: Трёхкомнатная квартира | | | |
|---|---|---|---|---|---|---|---|---|
| | Лист | № док. | Подпись | Дата | Спецификация сантехнического оборудования | Стадия | Лист | Листов |
| Дизайнер | Кырлан А.С. | | | 05.10.26 | | П | 16 | 89 |

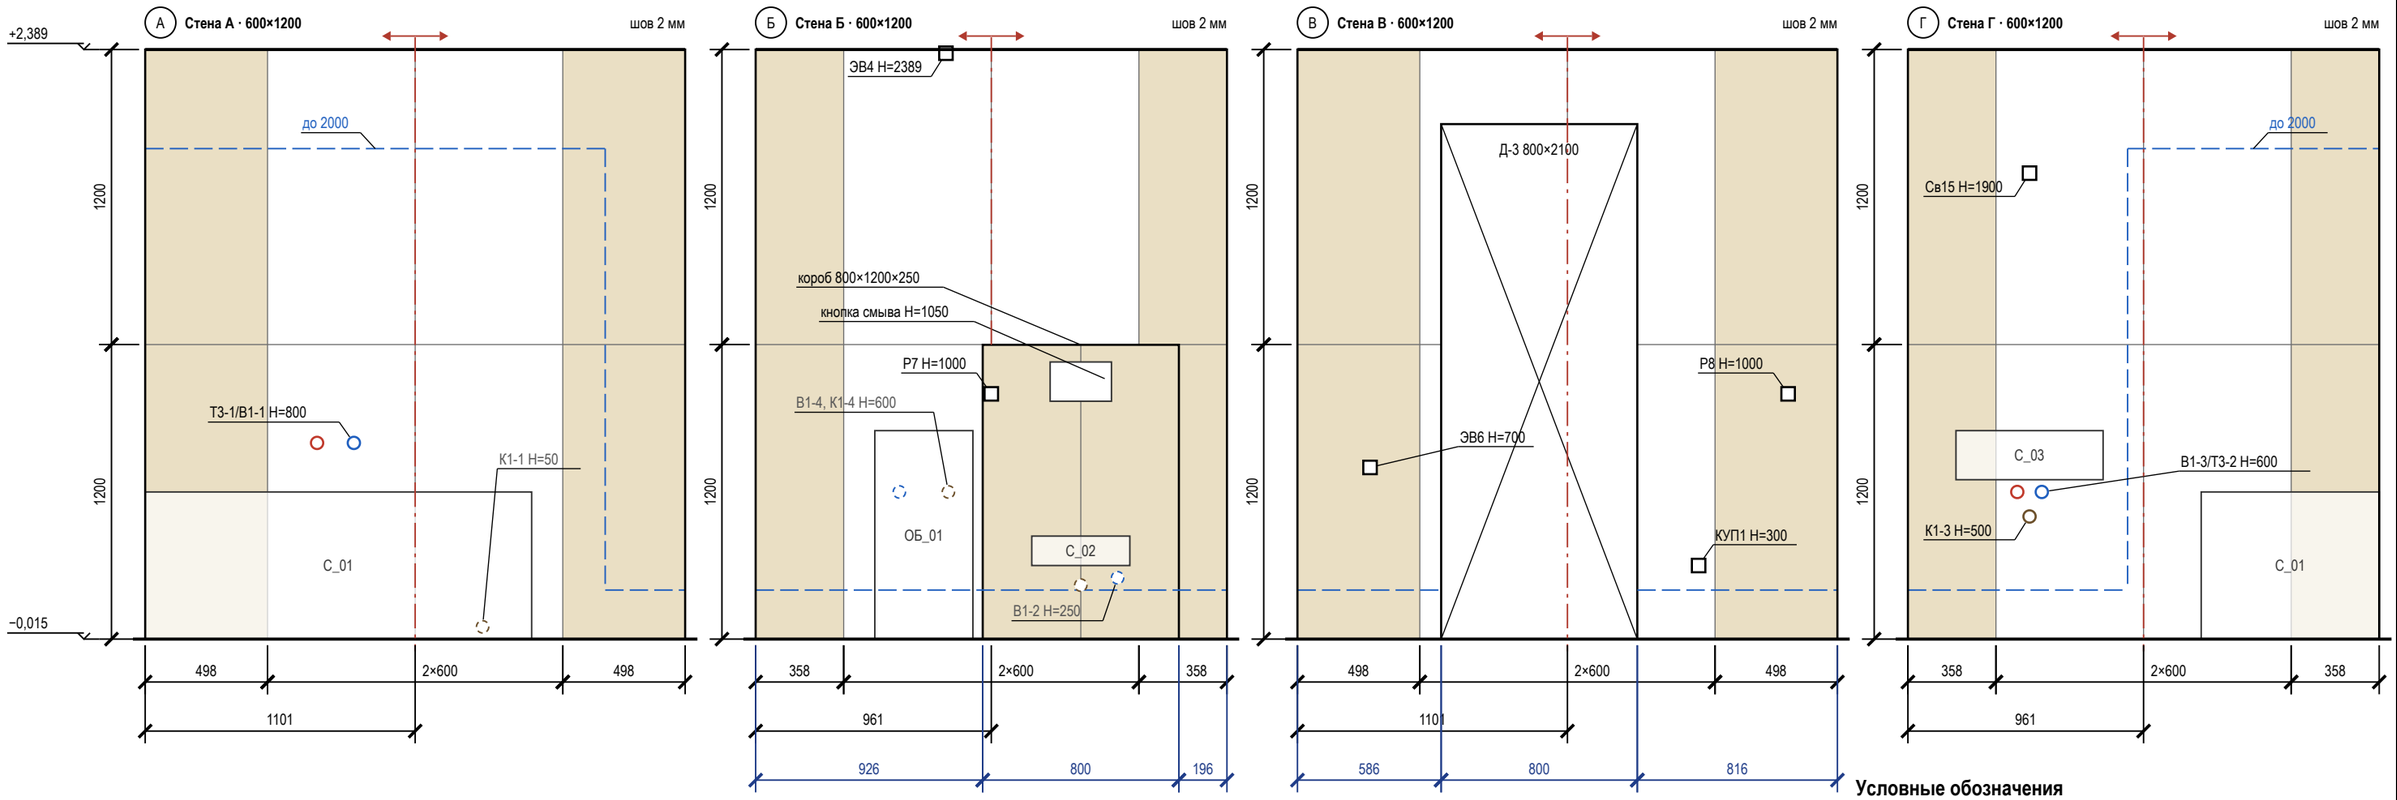


## Подсчёт плитки по стенам и коробу

| Поверхность | L × H, мм | S, м² | Целых | Подр. | С запасом | Подрезки: край / верх, мм |
|---|---|---|---|---|---|---|
| стена А | 2202 × 2404 | 5,41 | 4 | 4 | 9 | 498 / 498; целый ряд |
| стена Б | 1922 × 2404 | 3,78 | 2 | 5 | 8 | 358 / 358; целый ряд |
| короб (ст. Б) | 800×1200×250 | 1,76 | 0 | 6 | 7 | лицо 399 / 399; бок. 250 |
| стена В | 2202 × 2404 | 3,73 | 0 | 8 | 9 | 498 / 498; целый ряд |
| стена Г | 1922 × 2404 | 4,74 | 4 | 4 | 9 | 358 / 358; целый ряд |
| **Итого** | | **19,41** | **10** | **27** | **42** | |

## Сдвиг точек под раскладку

| Точка (ВК, ЭОМ) | Стена | Проект: от угла / Н | Под раскладку: от угла / Н | Сдвиг, мм |
|---|---|---|---|---|
| Т3-1/В1-1 | А | 776 / 800 | 800 / 800 | +24 в центр плитки |
| ЭВ4 | Б | 776 / 2389 | 660 / 2403 | −116 в центр плитки; Н +14 |
| КУП1 | В | 1636 / 300 | 1703 / 300 | +67 на шов |
| ЭВ6 | В | 296 / 700 | 198 / 700 | −98 в центр плитки |
| В1-3/Т3-2, К1-3, Св15 | Г | 496 / 600, 500, 1900 | 359 / 600, 500, 1900 | −137 на шов |

## Примечания

1. Вид изнутри, стены по часовой стрелке А → Г. Высоты — от чистого пола (−0,015), отметки — от ±0,000. Раскладка от чистовых размеров (штукатурка 10 + клей 5 + плитка 9 мм), подрезки чистые; старт — от оси стены, ряды от пола целыми.
2. Облицовка до потолка (+2,389).
3. Точки из таблицы сдвигов переносятся до черновой разводки: смеситель — по оси пары В1 + Т3; вывод на оси прибора — вместе с прибором, иначе старт раскладки — на ось прибора.
4. За приборами и в коробе (К1-1, В1-2, К1-2, В1-4, К1-4) — штриховым кольцом.
5. Гидроизоляция: 200 мм от ЧП по периметру; над ванной — до 2000 и 300 мм за борт (СП 29.13330.2011, п. 7.2 — на высоту замачивания); углы — лентой; акт скрытых работ, пролив.
6. Короб 800×1200×250: лицо 399 / 399 мм от оси кнопки смыва, боковины, полка; углы — запил 45° или профиль; за коробом плитку не кладут.
7. Между коробом и углом полоса 196 мм — довести короб до угла.

## Условные обозначения

- плитка целая; тонкая линия — шов
- плитка с подрезкой (размер — на цепочке)
- ось старта; стрелки — направление укладки
- верх гидроизоляции: 200 от ЧП, в мокрой зоне — «до …»
- проём — не облицовывается
- сантехприбор: габарит, высота по практике
- короб инсталляции, в нём кнопка смыва 250×160
- вывод В1 (код — в ведомости привязок)
- вывод Т3 (код — в ведомости привязок)
- вывод К1 (код — в ведомости привязок)
- вывод за прибором / в коробе (не на сетке)
- электроточка: марка и Н — по листам ЭОМ
- отметка уровня, м: ±0,000 — чистый пол жилых помещений
- низ потолка; серая полоса — стена без плитки
- А — обозначение стены А–Г (как на развёртках)

| | | | | | |
|---|---|---|---|---|---|
| | | | | | Проект: Трёхкомнатная квартира |
| | Лист | № док. | Подпись | Дата | Раскладка плитки. Ванная. Развёртки стен |
| Дизайнер | Кырлан А.С. | | | 05.10.26 | |

| Стадия | Лист | Листов |
|---|---|---|
| П | 17 | 89 |

выпуск 05.10.2026 № 6a37468da7 · стр. 17 из 89

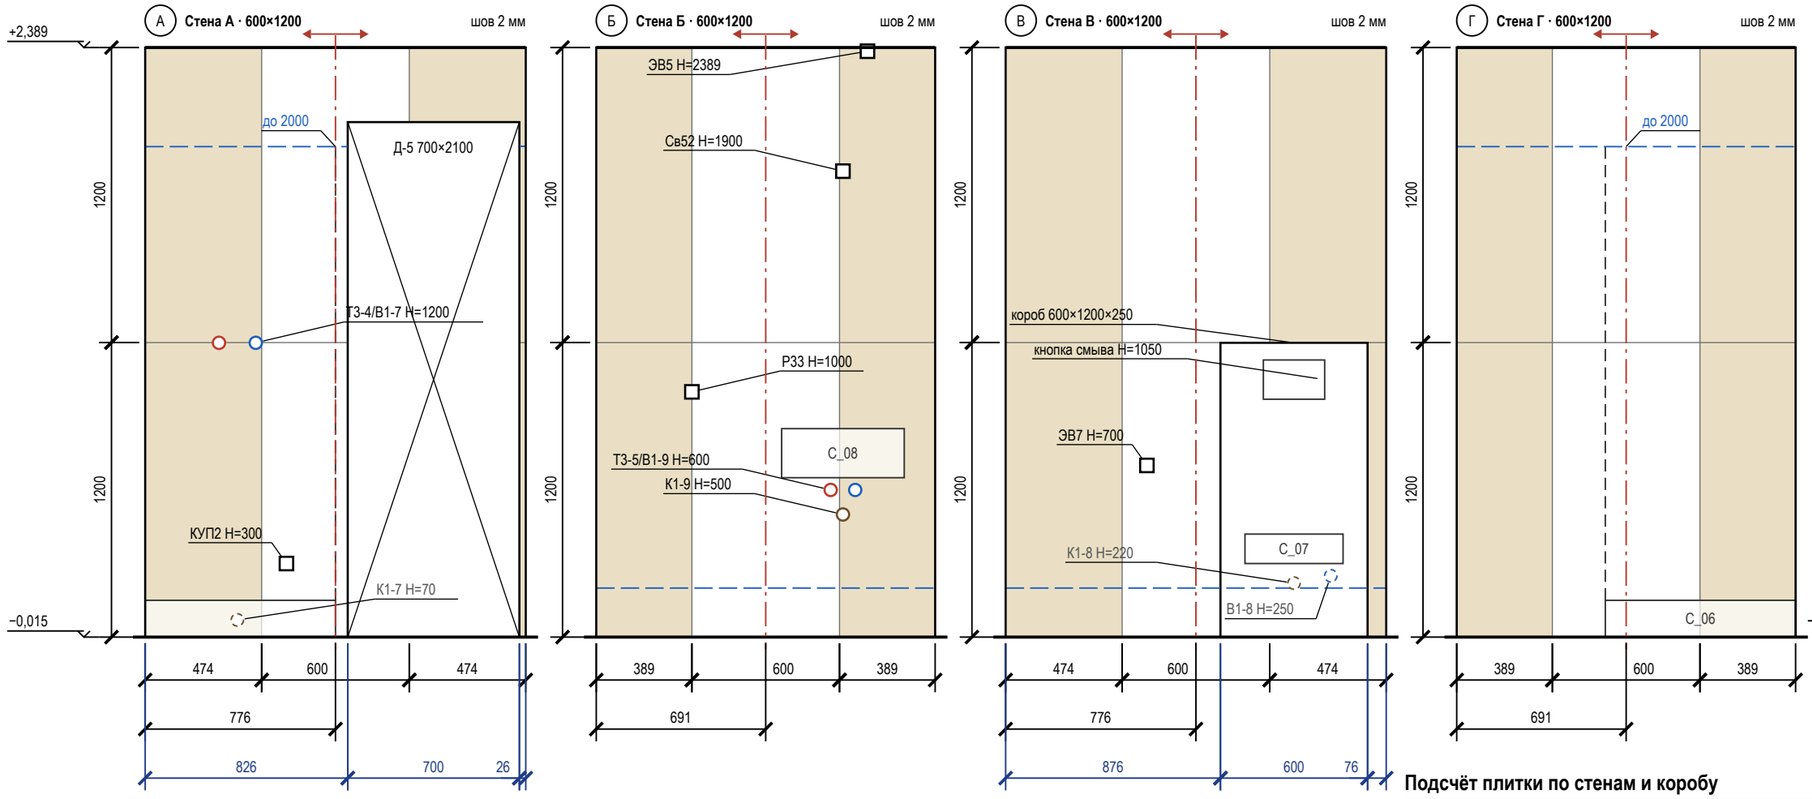


## Условные обозначения

- плитка целая; тонкая линия — шов
- плитка с подрезкой (размер — на цепочке)
- ось старта; стрелки — направление укладки
- верх гидроизоляции: 200 от ЧП, в мокрой зоне — «до …»
- проём — не облицовывается
- сантехприбор: габарит, высота по практике
- граница душевой зоны (ограждение)
- короб инсталляции, в нём кнопка смыва 250×160
- вывод В1 (код — в ведомости привязок)
- вывод Т3 (код — в ведомости привязок)
- вывод К1 (код — в ведомости привязок)
- вывод за прибором / в коробе (не на сетке)
- электроточка: марка и Н — по листам ЭОМ
- отметка уровня, м: ±0,000 — чистый пол жилых помещений
- низ потолка; серая полоса — стена без плитки
- (А) обозначение стены А–Г (как на развёртках)

## Примечания

1. Вид изнутри, стены по часовой стрелке А → Г. Высоты — от чистого пола (−0,015), отметки — от ±0,000. Раскладка от чистовых размеров (штукатурка 10 + клей 5 + плитка 9 мм), подрезки чистые; старт — от оси стены, ряды от пола целыми.
2. Облицовка до потолка (+2,389).
3. Точки из таблицы сдвигов переносятся до черновой разводки: смеситель — по оси пары В1 + Т3; вывод на оси прибора — вместе с прибором, иначе старт раскладки — на ось прибора.
4. За приборами и в коробе (К1-7, В1-8, К1-8) — штриховым кольцом.
5. Гидроизоляция: 200 мм от ЧП по периметру; у душа — до 2000 и 500 мм за поддон (СП 29.13330.2011, п. 7.2 — на высоту замачивания); углы — лентой; акт скрытых работ, пролив.
6. Короб 600×1200×250: лицо 600 мм от оси кнопки смыва, боковины, полка; углы — запил 45° или профиль; за коробом плитку не кладут.
7. Между коробом и углом полоса 76 мм — довести короб до угла.

## Подсчёт плитки по стенам и коробу

| Поверхность | L × H, мм | S, м² | Целых | Подр. | С запасом | Подрезки: край / верх, мм |
|---|---|---|---|---|---|---|
| стена А | 1552 × 2404 | 2,38 | 0 | 6 | 7 | 474 / 474; целый ряд |
| стена Б | 1382 × 2404 | 3,44 | 2 | 4 | 7 | 389 / 389; целый ряд |
| стена В | 1552 × 2404 | 3,13 | 1 | 5 | 7 | 474 / 474; целый ряд |
| короб (ст. В) | 600×1200×250 | 1,47 | 1 | 3 | 5 | лицо 600; бок. 250 |
| стена Г | 1382 × 2404 | 3,44 | 2 | 4 | 7 | 389 / 389; целый ряд |
| **Итого** | | **13,85** | **6** | **22** | **33** | |

## Сдвиг точек под раскладку

| Точка (ВК, ЭОМ) | Стена | Проект: от угла / Н | Под раскладку: от угла / Н | Сдвиг, мм |
|---|---|---|---|---|
| Т3-4/В1-7 | А | 376 / 1200 | 475 / 1141 | +99 на шов; Н −59 |
| КУП2 | А | 576 / 300 | 475 / 300 | −101 на шов |
| Т3-5/В1-9, К1-9, Св52 | Б | 1006 / 600, 500, 1900 | 992 / 600, 500, 1900 | −14 на шов |
| ЭВ5 | Б | 1106 / 2389 | 992 / 2343 | −114 на шов; Н −46 |
| ЭВ7 | В | 576 / 700 | 475 / 700 | −101 на шов |

| | | | | | |
|---|---|---|---|---|---|
| | Лист | № док. | Подпись | Дата | Проект: Трёхкомнатная квартира |
| Дизайнер | Кырлан А.С. | | | 05.10.26 | Раскладка плитки. Санузел 2. Развёртки стен |

| Стадия | Лист | Листов |
|---|---|---|
| П | 18 | 89 |

выпуск 05.10.2026 № 6a37468da7 · стр. 18 из 89

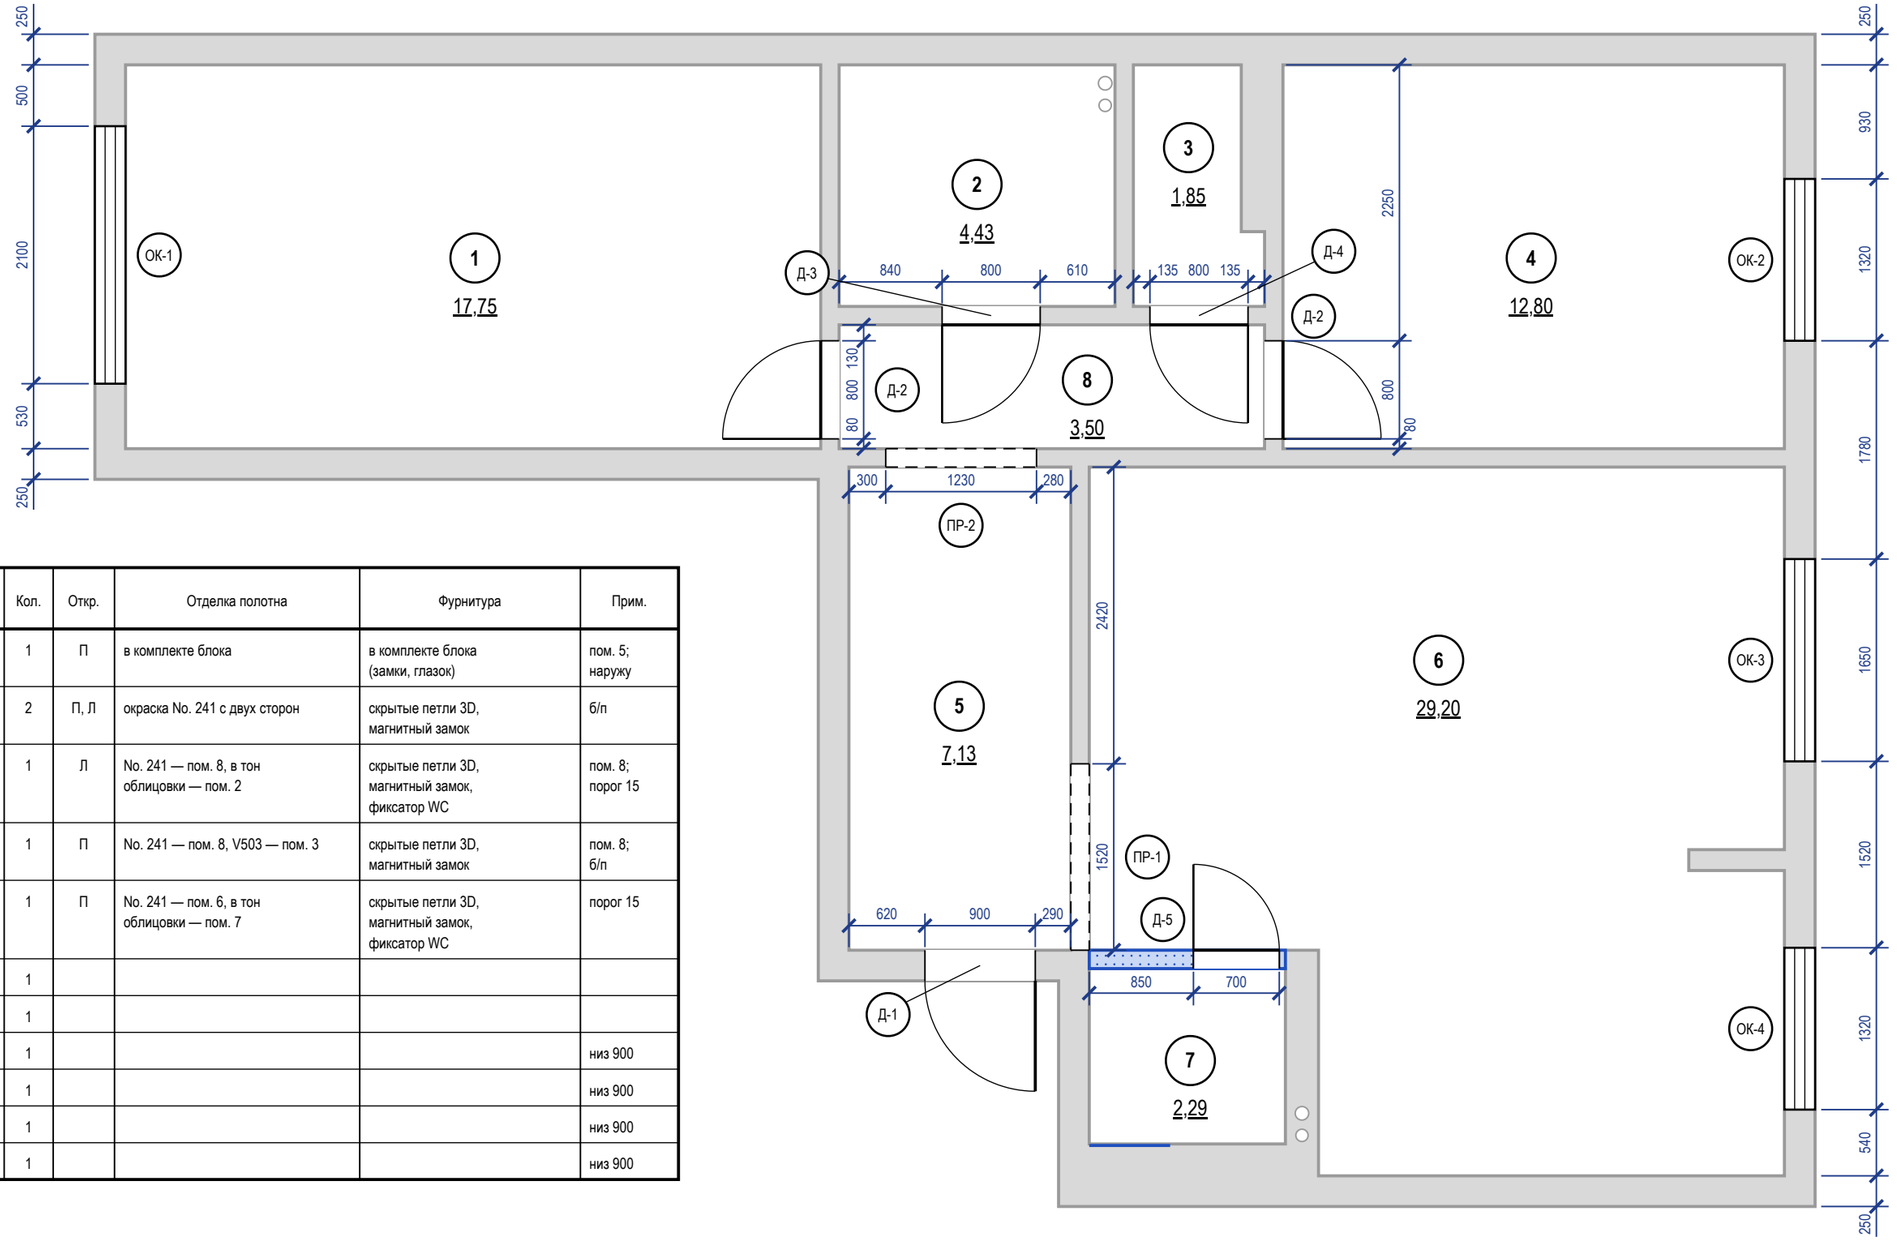


## Ведомость заполнения проёмов

| Марка | Наименование, обозначение | Проём ш×в, мм | Кол. | Откр. | Отделка полотна | Фурнитура | Прим. |
|---|---|---|---|---|---|---|---|
| Д-1 | Блок дверной входной, ГОСТ 31173-2016 | 900×2100 | 1 | П | в комплекте блока | в комплекте блока (замки, глазок) | пом. 5; наружу |
| Д-2 | Дверь скрытого монтажа, ТУ изготовителя | 800×2100 | 2 | П, Л | окраска No. 241 с двух сторон | скрытые петли 3D, магнитный замок | б/п |
| Д-3 | Дверь скрытого монтажа, ТУ изготовителя | 800×2100 | 1 | Л | No. 241 — пом. 8, в тон облицовки — пом. 2 | скрытые петли 3D, магнитный замок, фиксатор WC | пом. 8; порог 15 |
| Д-4 | Дверь скрытого монтажа, ТУ изготовителя | 800×2100 | 1 | П | No. 241 — пом. 8, V503 — пом. 3 | скрытые петли 3D, магнитный замок | пом. 8; б/п |
| Д-5 | Дверь скрытого монтажа, ТУ изготовителя | 700×2100 | 1 | П | No. 241 — пом. 6, в тон облицовки — пом. 7 | скрытые петли 3D, магнитный замок, фиксатор WC | порог 15 |
| ПР-1 | Портал без заполнения | 1520×2500 | 1 | | | | |
| ПР-2 | Портал без заполнения | 1230×2100 | 1 | | | | |
| ОК-1 | Блок оконный существующий | 2100×1500 | 1 | | | | низ 900 |
| ОК-2 | Блок оконный существующий | 1320×1500 | 1 | | | | низ 900 |
| ОК-3 | Блок оконный существующий | 1650×1500 | 1 | | | | низ 900 |
| ОК-4 | Блок оконный существующий | 1320×1400 | 1 | | | | низ 900 |

## Примечания

1. Размеры проёмов и привязки — в миллиметрах от чистых граней стен до отделки; привязка — от угла того помещения, со стороны которого стоит размер. Размер в ведомости — ширина × высота проёма от чистого пола 0,000. Откос от угла помещения до проёма с коробкой — не менее 50 мм.
2. Марки в кружках — типы заполнения проёмов (ГОСТ 21.501-2018, п. 5.3.2); одна марка — один типоразмер; количество сверено с планом.
3. Открывание: Л — петли слева, П — справа, если смотреть со стороны, куда открывается полотно (на себя).
4. Скрытые двери (Д-2…Д-5): проём замерить в чистоте; блок заказать до штукатурки (≈ 30 дн.), короб ставить до штукатурки; полотно навесить после чистовой отделки, красить в цвет стен. Порядок практика монтажа, изготовитель подтверждает.
5. Д-2…Д-4 — существующие проёмы, до техзаключения не расширять. Д-3, Д-4: стена принята 150 мм, по скану 85 мм, не замерено; узел — для 150 мм.
6. Окна ОК-1…ОК-4 существующие, сохраняются; подоконники и откосы не заданы — приняты.
7. Размеры проёмов и привязки сняты со скана плана заказчика и на объекте не замерены (обмерный план — лист 3).
8. Экспликация помещений — лист 3; в марках помещений — номер и площадь, м².
9. Привязка проёма к углу помещения меньше 1 мм на листе, размер на плане не показан: Д-5 — 50 мм.

| | | | | | Проект: Трёхкомнатная квартира | | | |
|---|---|---|---|---|---|---|---|---|
| | Лист | № док. | Подпись | Дата | | | | |
| Дизайнер | Кырлан А.С. | | | 05.10.26 | План размещения дверей | Стадия | Лист | Листов |
| | | | | | | П | 19 | 89 |

выпуск 05.10.2026 № 6a37468da7 · стр. 19 из 89

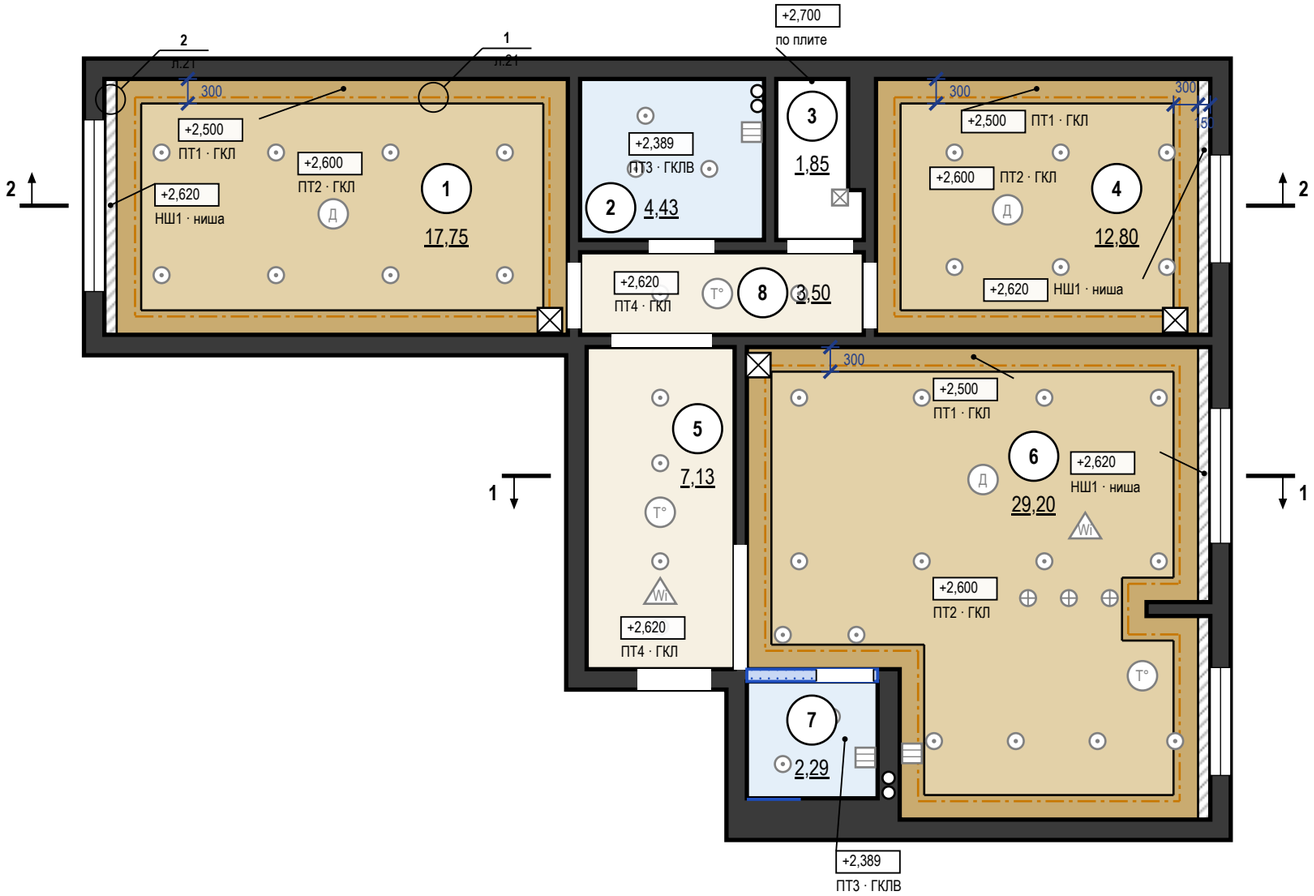


## Ведомость потолков

| Пом. | Марка | Конструкция | Низ | S, м² | Q |
|---|---|---|---|---|---|
| 1 | ПТ1 | ГКЛ П113, короб LED | +2,500 | 4,83 | Q3 |
| 1 | ПТ2 | ГКЛ П113 | +2,600 | 12,45 | Q3 |
| 1 | НШ1 | ниша под шторы 150×120 | +2,620 | 0,47 | |
| 2 | ПТ3 | ГКЛВ П113 | +2,389 | 4,43 | Q3 |
| 3 | | по плите, окраска | +2,700 | 1,85 | |
| 4 | ПТ1 | ГКЛ П113, короб LED | +2,500 | 3,88 | Q3 |
| 4 | ПТ2 | ГКЛ П113 | +2,600 | 8,45 | Q3 |
| 4 | НШ1 | ниша под шторы 150×120 | +2,620 | 0,47 | |
| 5 | ПТ4 | ГКЛ П113 | +2,620 | 7,13 | Q3 |
| 6 | ПТ1 | ГКЛ П113, короб LED | +2,500 | 6,80 | Q3 |
| 6 | ПТ2 | ГКЛ П113 | +2,600 | 21,56 | Q3 |
| 6 | НШ1 | ниша под шторы 150×120 | +2,620 | 0,84 | |
| 7 | ПТ3 | ГКЛВ П113 | +2,389 | 2,29 | Q3 |
| 8 | ПТ4 | ГКЛ П113 | +2,620 | 3,50 | Q3 |
| | | **Итого** | | **78,95** | |

## Ведомость вырезов и закладных в потолке

| Марка | Устройство | Кол. | Пом. |
|---|---|---|---|
| | Светильник встраиваемый (марки — план освещения) | 39 | 1, 2, 4, 5, 6, 7, 8 |
| | Светильник накладной (марки — план освещения) | 1 | 3 |
| | Светильник подвесной (марки — план освещения) | 3 | 6 |
| ИП1, ИП2, ИП4 | Извещатель дымовой | 3 | 1, 4, 6 |
| ИП3, ИП5, ИП6 | Извещатель тепловой | 3 | 5, 6, 8 |
| АР1, АР2 | Точка доступа Wi-Fi, PoE | 2 | 5, 6 |
| ВР1…ВР3 | Решётка вытяжная (вентилятор) | 3 | 2, 6, 7 |
| | Люк ревизии 300×300 | 3 | 1, 4, 6 |

## Примечания

1. За отметку ±0,000 принят уровень чистого пола сухих помещений (готовое покрытие), а не существующего пола; пол пом. 2, 7 — −0,015; верх плиты перекрытия −0,064 — расчётный по пирогу пола, не замерен; существующий пол снимается до плиты, его отметка не замерена. Отметки в прямоугольниках — низ потолка; низ плиты перекрытия +2,700. Марка потолка — одна конструкция и отметка на весь альбом.
2. Потолки ГКЛ — каркасная система П113: подвесы через 1000, несущие профили через 500, основные через 1200 мм; листы — поперёк несущих профилей. В помещениях 2, 7 — ГКЛВ на оцинкованном каркасе.
3. Нижний уровень — пояс-короб по периметру шириной 300 мм (карниз подсветки + 150 мм полки), верхний — поле внутри пояса.
4. LED-лента в алюминиевом профиле посередине карниза короба шириной 300 мм (узел 1, лист 21); длина по плану: пом. 1 — 15,5 м (в плане освещения 15,5); пом. 4 — 12,3 м (в плане освещения 12,3); пом. 6 — 22,1 м (в плане освещения 22,1).
5. Ниши под шторы 150×120 мм — на всю длину стены с окном; карниз — на закладной до обшивки (узел 2, лист 21).
6. Примыкание к стенам: теневой шов 15 мм, техзазор 3 мм — пом. 1, 4, 6, по стенам, выровненным штукатуркой (узел 1); пом. 2, 5, 7, 8 разделительная лента.
7. Светильники и потолочные устройства — подложка с планов освещения, слаботочных систем и вентиляции (положение — по ним); вырезы и закладные — по ведомости на листе, до обшивки; отверстия не совмещать с профилями, глубина корпуса светильника до 70 мм.
8. Разрезы 1–1, 2–2 и узлы — на листе 21; высоты мебели и дверных блоков сверены с низом потолка в разрезах.
9. Шпаклевание ГКЛ и условия приёмки — Q3: рассеянный дневной свет, осмотр с 2 м; боковой свет не оценивается.
10. Люки ревизии 300×300 мм — по центру блоков питания LED (БП1, БП2, БП4; координаты — план освещения).
11. Пом. 3 — потолок по плите без подвесной системы; отделка — по ведомости отделки.

| | | | | | |
|---|---|---|---|---|---|
| | | | | | Проект: Трёхкомнатная квартира |
| | Лист | № док. | Подпись | Дата | План потолков |
| Дизайнер | Кырлан А.С. | | | 05.10.26 | Стадия: П; Лист: 20; Листов: 89 |

выпуск 05.10.2026 № 6a37468da7 · стр. 20 из 89

## Разрез 1–1 (М 1:40)

Пом. 6 Кухня-гостиная; линия разреза — план потолков, лист 20

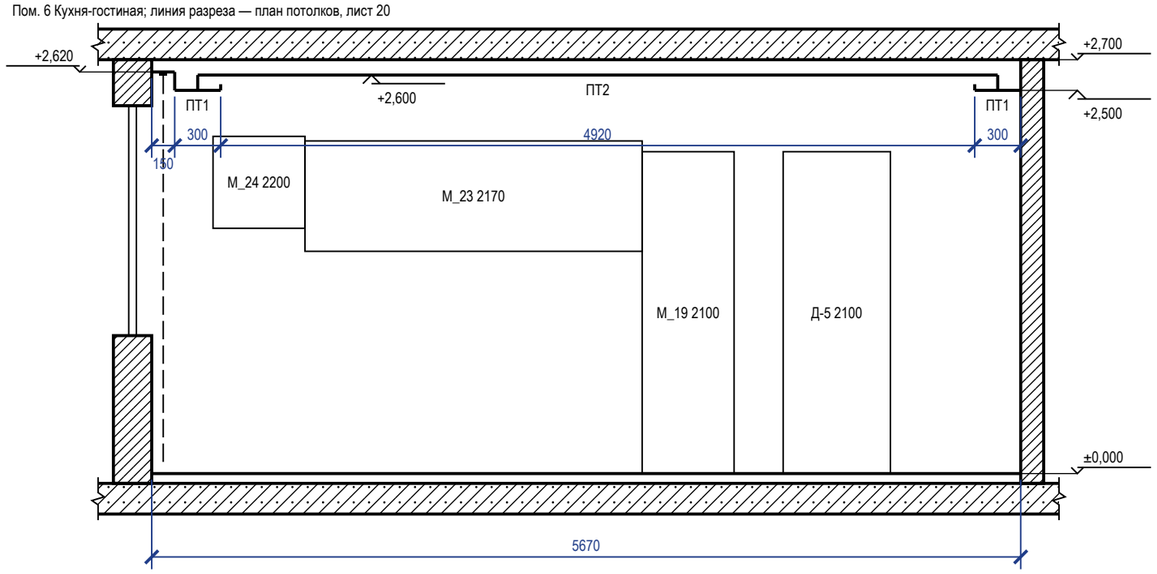


## Разрез 2–2 (М 1:40)

Пом. 1 Спальня 1; линия разреза — план потолков, лист 20

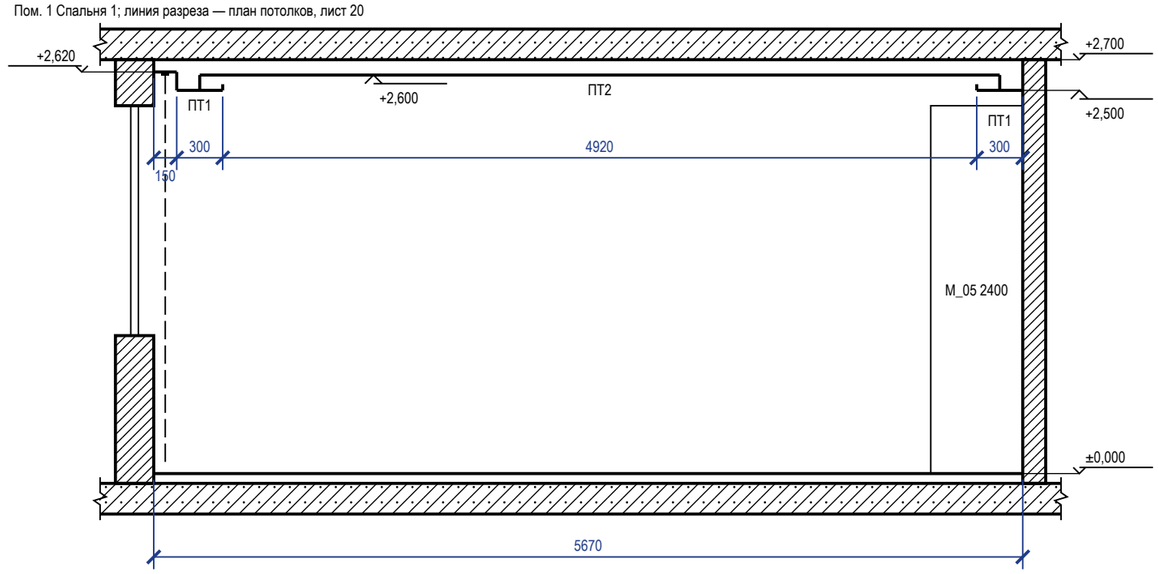


## 1 Короб с LED-подсветкой, теневой шов (М 1:10)

Пом. 1, 4, 6; карниз 150×100, щель под свет 60 мм

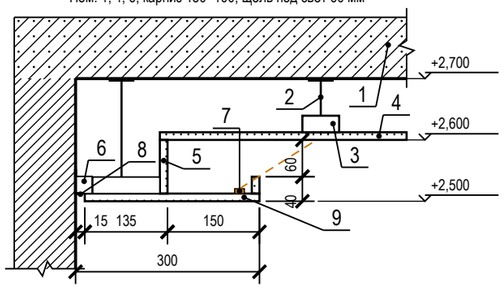


1 — плита перекрытия
2 — подвес прямой, шаг 1000 мм
3 — ПП 60×27: несущие через 500, основные через 1200 мм
4 — ГКЛ 12,5 по П113 — верхний уровень
5 — задняя стенка и бортик карниза — ГКЛ 12,5
6 — ПН 28×27 по периметру, к стене через 500 мм
7 — LED-лента в алюминиевом профиле
8 — теневой профиль: шов 15 мм, зазор 3 мм
9 — низ короба — ГКЛ 12,5 по ПП 60×27

## 2 Ниша под шторы (М 1:10)

Пом. 1, 4, 6; без подсветки; закладные под карниз — до обшивки

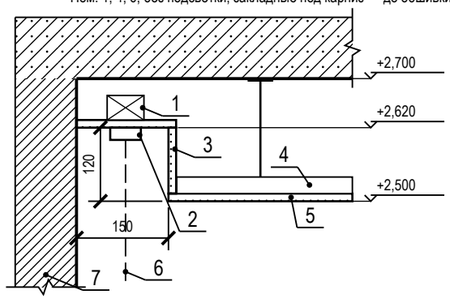


1 — закладная под карниз — брус 40×50
2 — карниз (шина), высота с верхом портьеры 100 мм
3 — стенка и потолок ниши — ГКЛ 12,5
4 — ПП 60×27 — каркас короба
5 — низ короба нижнего уровня — ГКЛ 12,5
6 — портьера
7 — стена с окном

## Условные обозначения

- плита перекрытия в сечении
- стена в сечении
- потолок ГКЛ в сечении; под линией — марка потолка (план потолков)
- мебель и дверные проёмы за секущей плоскостью; число — марка и верх от чистого пола, мм
- портьера в нише под шторы

## Примечания

1. Разрезы — по линиям 1–1, 2–2 на плане потолков (лист 20). Отметки — от ±0,000 чистого пола, м; размеры — мм.
2. Высоты мебели и дверных блоков за секущей плоскостью сверены с низом потолка над ними: верх ниже низа короба и поля.
3. ГКЛ 12,5 мм по каркасу П113; перепад уровней и бортик карниза — ГКЛ по ПП 60×27 (узел 1). Ниша под шторы — на всю длину стены с окном, карниз на закладной до обшивки (узел 2).
4. Толщины плит перекрытия и пирога пола показаны условно.

| | | | | | |
|---|---|---|---|---|---|
| | | | | | Проект: Трёхкомнатная квартира |
| | Лист | № док. | Подпись | Дата | |
| Дизайнер | Кырлан А.С. | | | 05.10.26 | Разрезы и узлы потолков |
| | | | | | Стадия: П; Лист: 21; Листов: 89 |

выпуск 05.10.2026 № 6a37468da7 · стр. 21 из 89

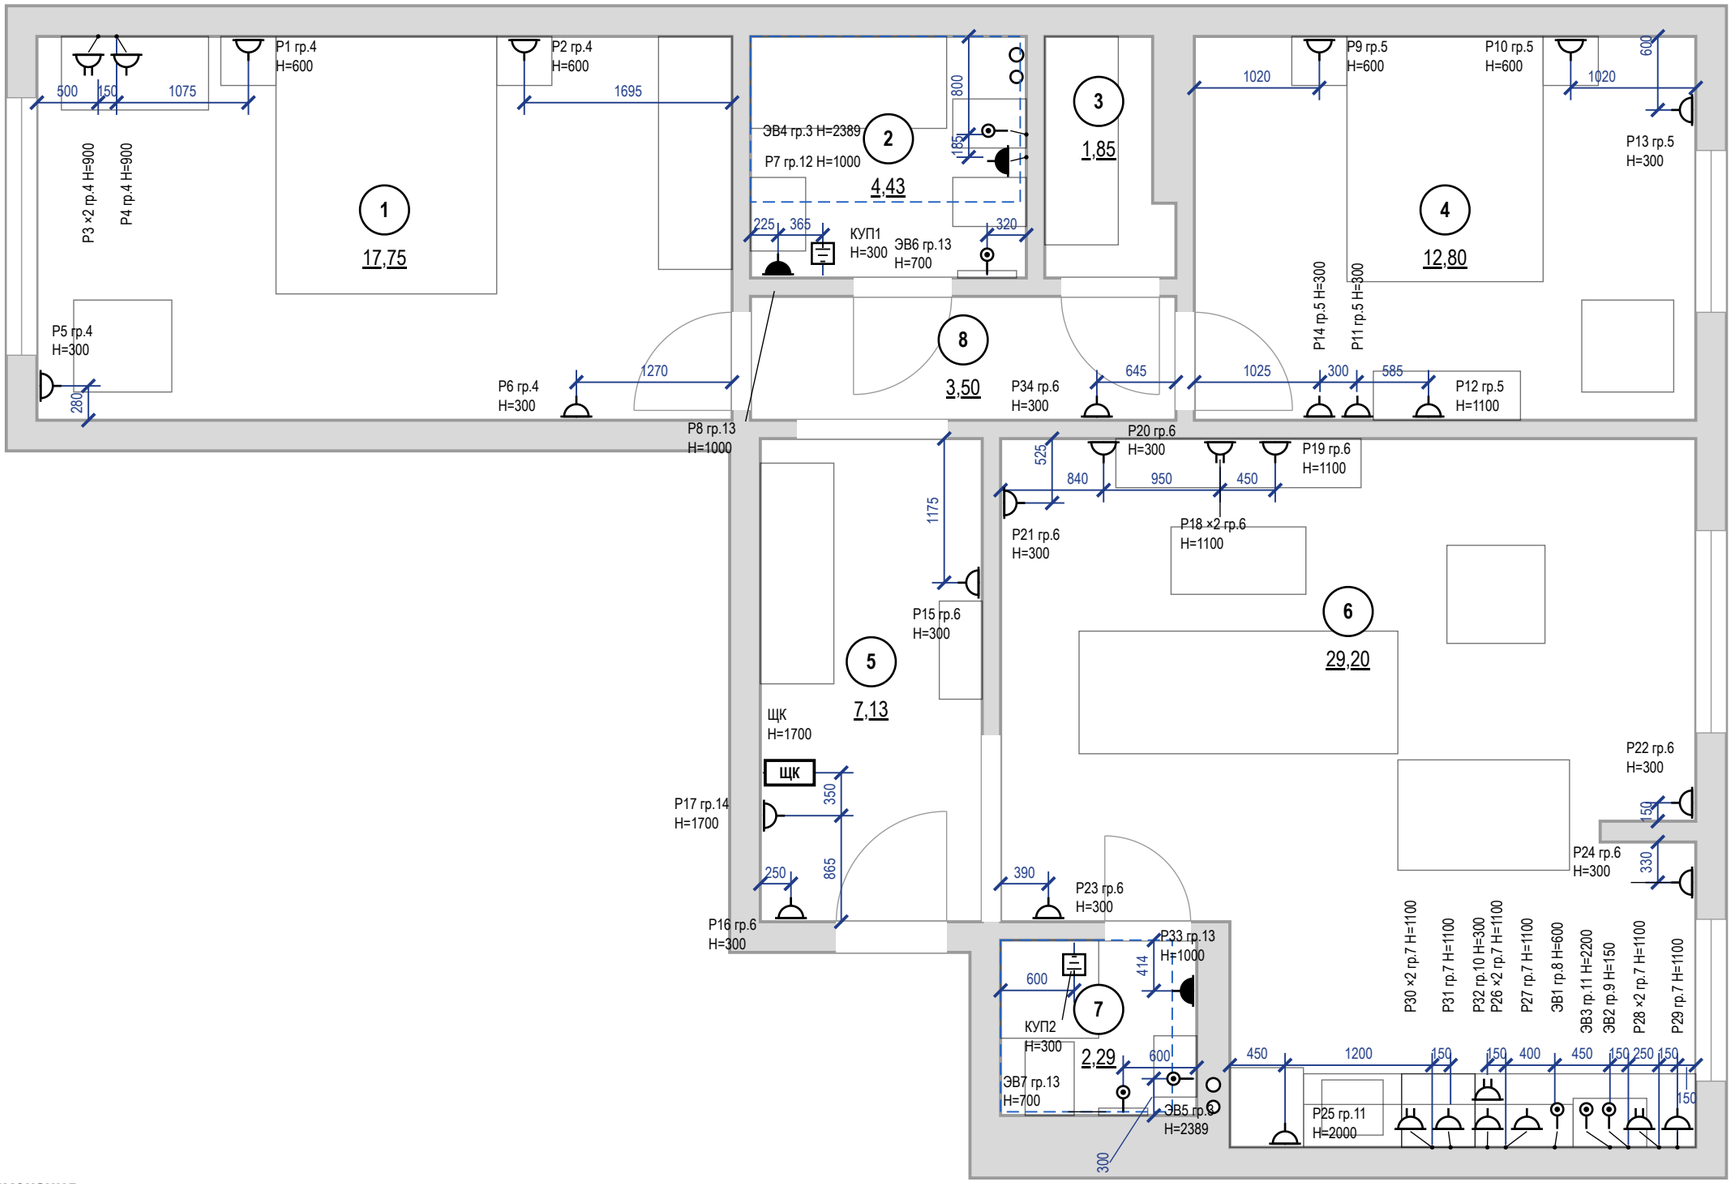


## Условные обозначения

- розетка с заземляющим контактом; у знака — марка, ×N постов в рамке, гр. — группа щита, Н — высота оси, мм
- то же, рамка на 2 поста (число черточек — число постов)
- розетка влагозащищённая IP44
- вывод кабеля для подключения прибора (без розетки), марка ЭВ
- КУП — коробка уравнивания потенциалов (ДСУП), проводник к шине РЕ щита
- ЩК — щит квартирный
- знак разведён для читаемости: точка на стене — у выноски, привязка — до неё
- граница зоны 2 ванной (600 мм от ванны/поддона)
- мебель и сантехприборы — подложка
- стояк: К1 — канализация, В1 — ХВС, Т3 — ГВС
- 1 — номер помещения, площадь м²

## Примечания

1. За отметку 0,000 принят уровень чистого пола. Высоты Н — от чистого пола до оси изделия; привязки — от чистовой грани стены до оси механизма (у рамки на несколько постов — до оси рамки).
2. Высота установки, не указанная на плане: розетки — 300 мм от чистого пола; выводы кабеля — по паспорту прибора.
3. Розетки в санузле — только вне зон 0–2 (ПУЭ 7.1.48, ГОСТ Р 50571.7.701-2024), IP44, через УЗО 30 мА.
4. Розеточные и мокрые линии — через УЗО или дифавтомат с током утечки не более 30 мА (ПУЭ 7.1.79); в санузле выполнить ДСУП (ПУЭ 7.1.87–7.1.88).
5. Кабель — медный, исполнение нг(А)-LS (ГОСТ 31565-2012); скрытая прокладка только горизонтально и вертикально, фактические трассы зафиксировать исполнительной схемой до закрытия отделкой.
6. Расчёт нагрузок, токов КЗ, селективности и сечений — по проекту ЭОМ организации с допуском СРО; лист задаёт состав, расположение и группы.
7. Выводы кухонной техники — после утверждения проекта кухни (ориентировочно); привязки выводов даны от осей модулей гарнитура и пересматриваются вместе с проектом кухни.
8. Электрический тёплый пол проектом не предусмотрен; при решении заказчика устроить — отдельный лист «План тёплых полов»: контуры с отступом 100 мм от стен и мебели без ножек, датчик в гофре, терморегулятор, своя группа щита через УЗО 30 мА.
9. Ведомости электроточек, изделий, светильников и расшифровка клавиш — лист «Ведомость электроточек и изделий».

| | | | | | |
|---|---|---|---|---|---|
| | | | | | Проект: Трёхкомнатная квартира |
| | Лист | № док. | Подпись | Дата | |
| Дизайнер | Кырлан А.С. | | | 05.10.26 | План розеток и электровыводов |

| Стадия | Лист | Листов |
|---|---|---|
| П | 22 | 89 |

выпуск 05.10.2026 № 6a37468da7 · стр. 22 из 89

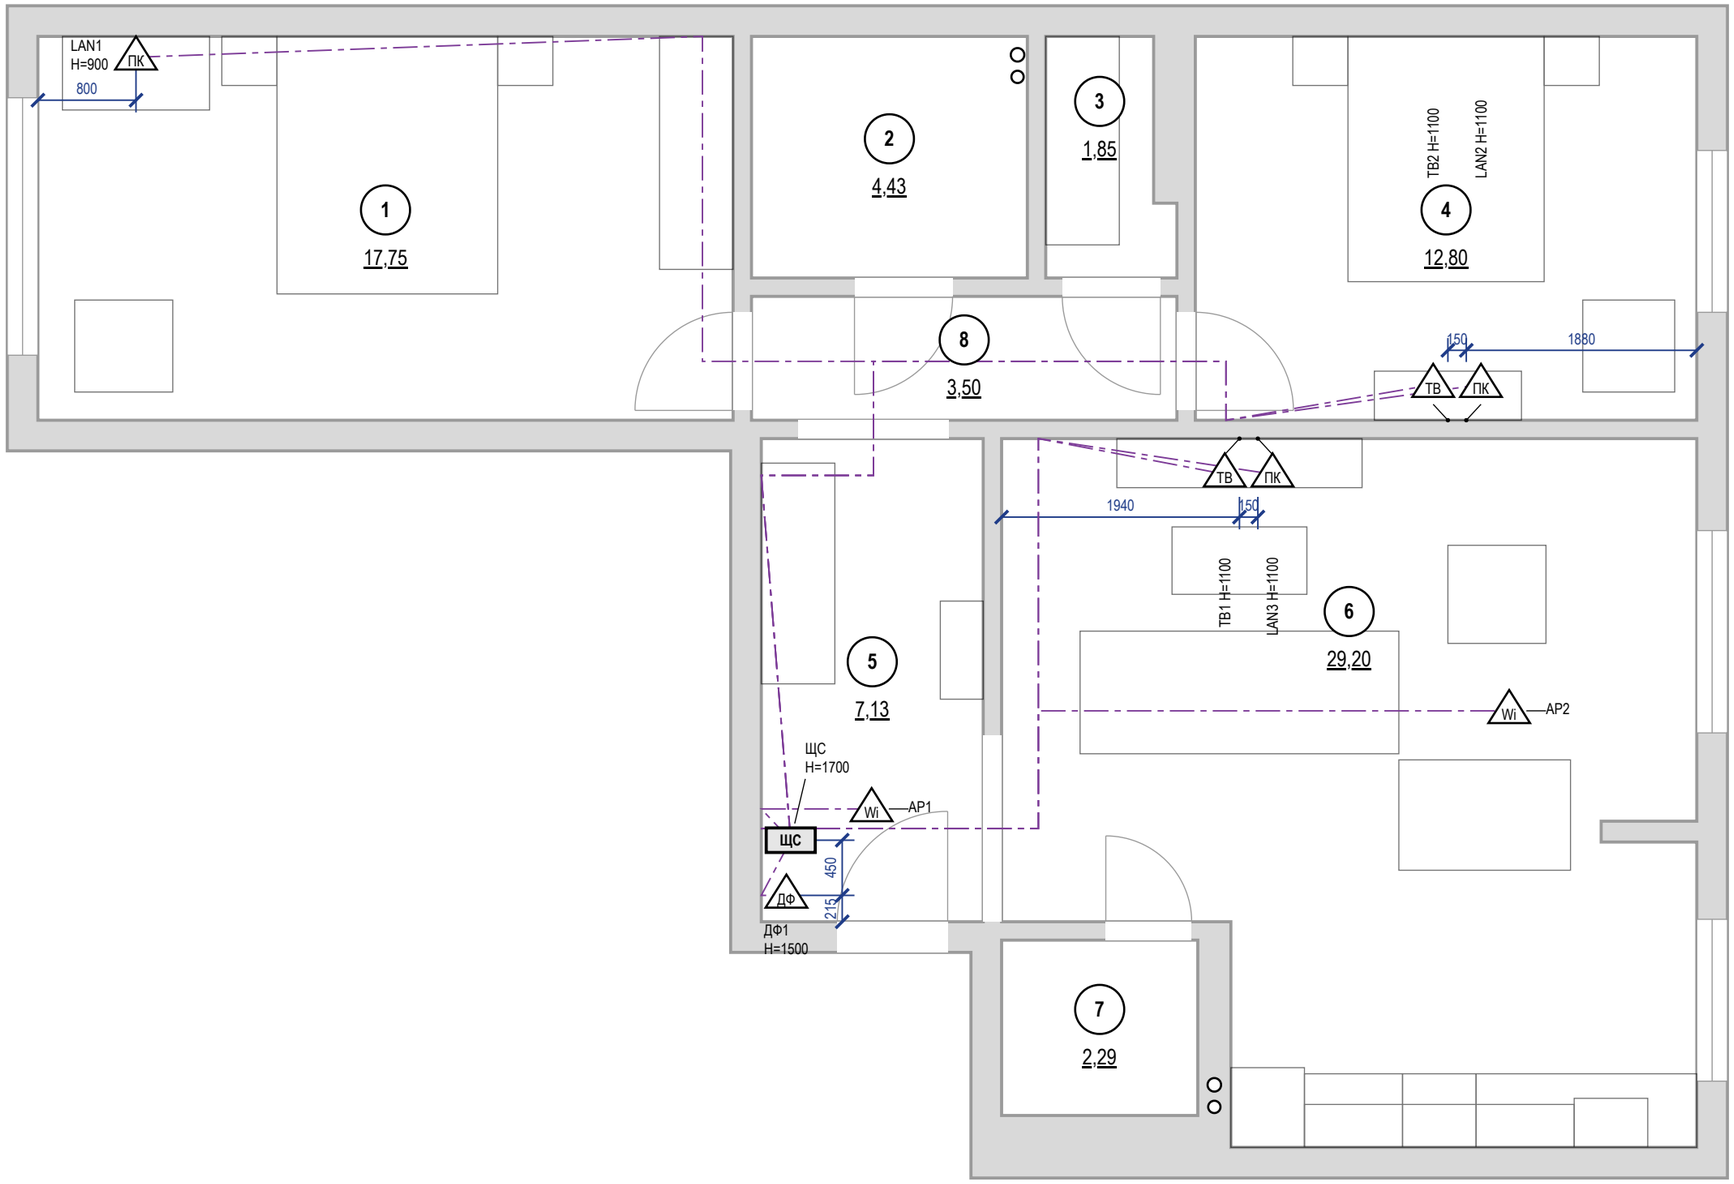


## Примечания

1. За отметку 0,000 принят уровень чистого пола. Высоты Н — от чистого пола до оси изделия; привязки — от чистовой грани стены до оси механизма (у рамки на несколько постов — до оси рамки).
2. Высота установки, не указанная на плане: розетки LAN и ТВ — 300 мм от чистого пола.
3. Слаботочные кабели — отдельно от силовых: в своей трубе или лотке, при параллельной прокладке не ближе 100 мм к силовым, пересечения под прямым углом; каждую точку — отдельным кабелем от ЩС без скруток.
4. Трассы на листе — принципиальные; фактические зафиксировать исполнительной схемой до закрытия отделкой. Силовые линии, УЗО 30 мА, ДСУП, кабель нг(А)-LS — по листам розеток и щита.
5. Проект силовой части и расчёт токов КЗ — по проекту ЭОМ; слаботочная часть согласуется с провайдером и управляющей компанией (домофон, коллективное ТВ).

| | | | | | |
|---|---|---|---|---|---|
| | | | | | Проект: Трёхкомнатная квартира |
| | Лист | № док. | Подпись | Дата | |
| Дизайнер | Кырлан А.С. | | | 05.10.26 | План слаботочных сетей |

| Стадия | Лист | Листов |
|---|---|---|
| П | 23 | 89 |

выпуск 05.10.2026 · 6a37468da7 · стр. 23 из 89

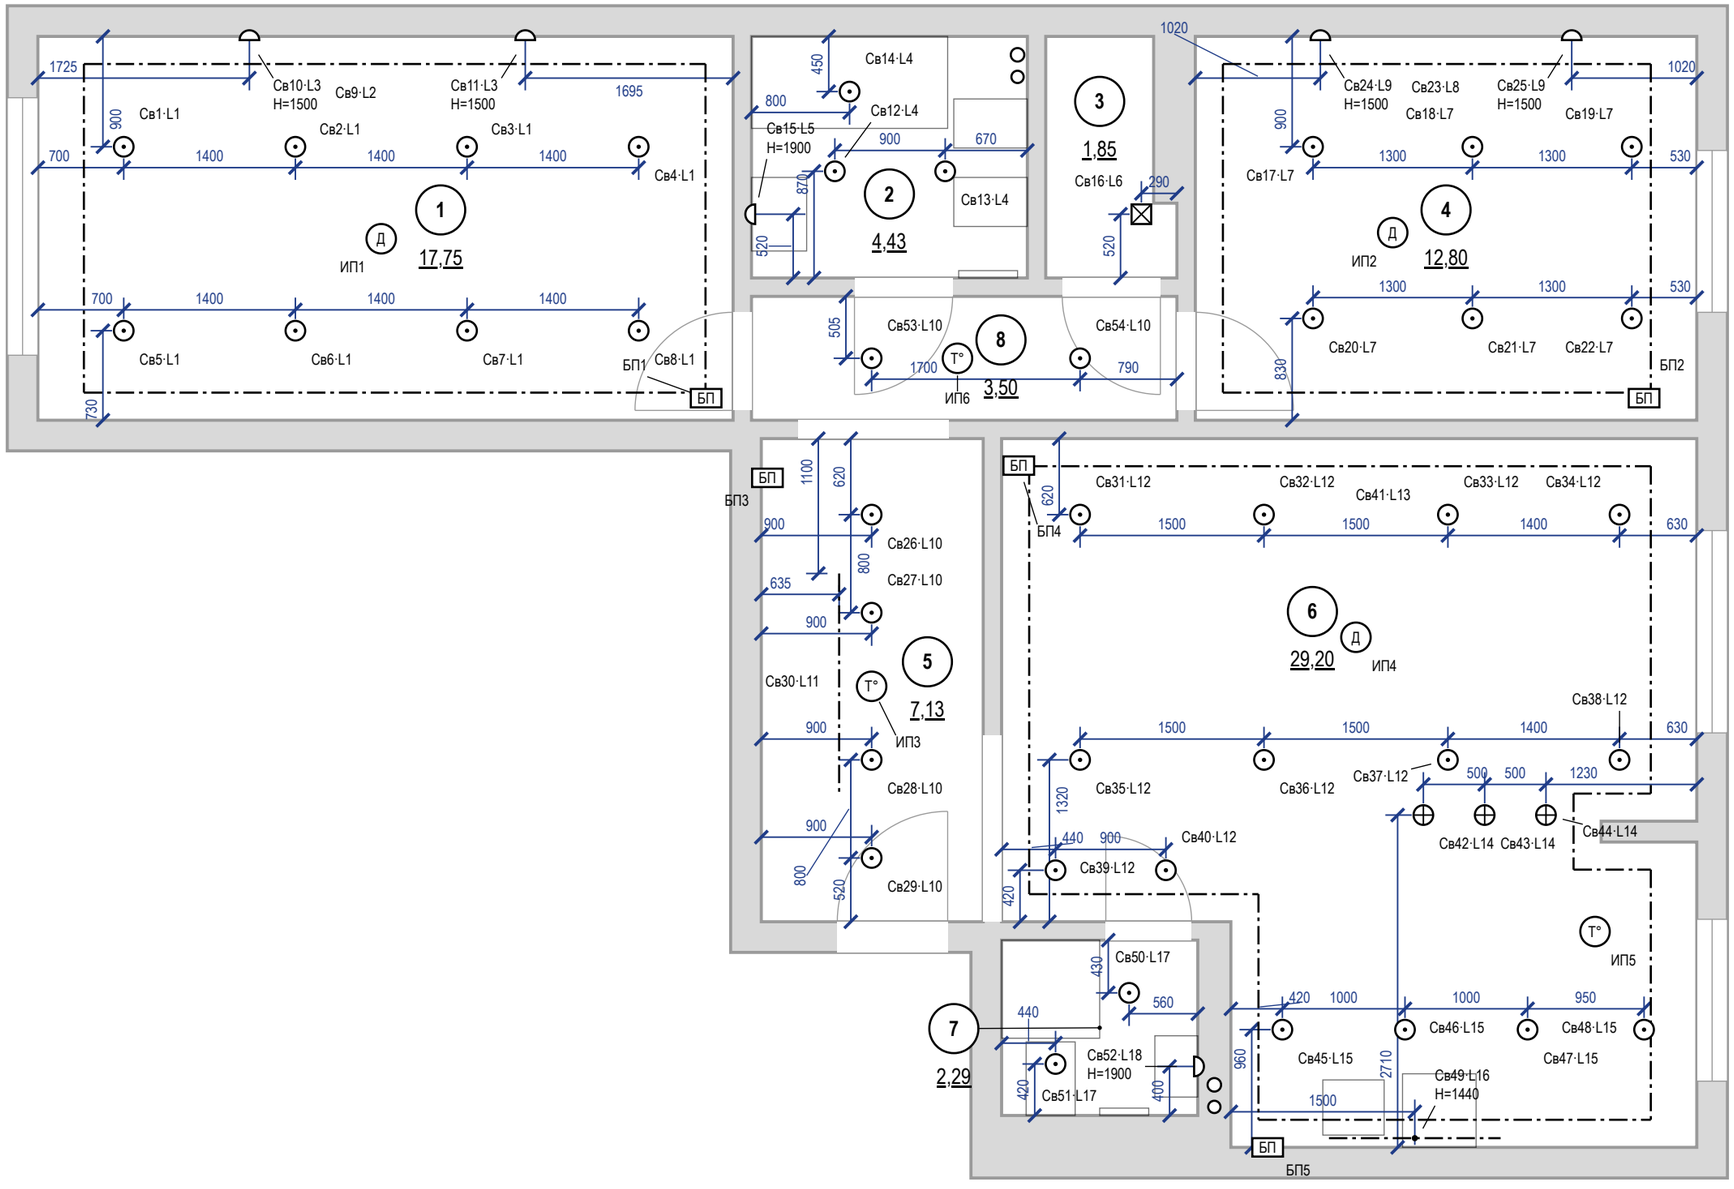


## Примечания

1. За отметку 0,000 принят уровень чистого пола. Высоты H — от чистого пола до оси изделия; привязки — от чистовой грани стены до оси механизма (у рамки на несколько постов — до оси рамки).
2. Высота установки, не указанная на плане: светильники — на потолке; настенные — по отметке H у знака. Привязки — до оси светильника от чистовой грани стены, по рядам.
3. Освещённость: Ен — СанПиН 1.2.3685-21, табл. 5.52 (на полу); Ф треб. = Ен·S/(U·MF) при U = 0,5 и MF = 0,71 (СП 52.13330.2016, табл. 4.3) — оценка, не светотехнический расчёт. Декоративная подсветка в Ф не входит.
4. Во влажных помещениях — светильники не ниже IP44; в зонах 0–2 ванной — по ГОСТ Р 50571.7.701-2024 (зона 1 — IPX5).
5. LED-лента в карнизе подсветки короба — по линии карниза с плана потолков; блок питания — в люке короба (БП на плане), питание ленты длиннее 5 м — с двух концов.
6. Розеточные и мокрые линии — через УЗО или дифавтомат с током утечки не более 30 мА (ПУЭ 7.1.79); в санузле выполнить ДСУП (ПУЭ 7.1.87–7.1.88).
7. Кабель — медный, исполнение нг(A)-LS (ГОСТ 31565-2012); скрытая прокладка только горизонтально и вертикально, фактические трассы зафиксировать исполнительной схемой до закрытия отделкой.
8. Расчёт нагрузок, токов КЗ, селективности и сечений — по проекту ЭОМ организации с допуском СРО; лист задаёт состав, расположение и группы.
9. Ведомость светильников — лист «Ведомость электроточек и изделий».

| | | | | | |
|---|---|---|---|---|---|
| | | | | | Проект: Трёхкомнатная квартира |
| | Лист | № док. | Подпись | Дата | План освещения |
| Дизайнер | Кырлан А.С. | | | 05.10.26 | |

| Стадия | Лист | Листов |
|---|---|---|
| П | 24 | 89 |

выпуск 05.10.2026 № 6a37468da7 · стр. 24 из 89

## Спецификация светильников

| Поз. | Марки | Наименование | Установка | Кол. | P, Вт | Σ P, Вт | Ф, лм | Тц, К | Ra | Угол, ° | IP | Дим. | Группа | Пом. |
|---|---|---|---|---|---|---|---|---|---|---|---|---|---|---|
| 1 | Св1–Св8 | Встраиваемый точечный | в ГКЛ, корпус ≤ 70 мм | 8 | 12 | 96 | 1000 | 2700 | 90 | — | 20 | — | L1 | 1 |
| 2 | Св9 | Лента светодиодная 24 В | в карнизе короба, профиль с рассеивателем | 15,5 м | 9,6/м | 148,8 | 900/м | 2700 | 90 | — | 20 | да | L2 | 1 |
| 3 | Св10, Св11, Св24, Св25 | Настенный (бра) | на стене, H=1500 | 4 | 6 | 24 | 400 | 2700 | 90 | 60 | 20 | — | L3, L9 | 1, 4 |
| 4 | Св12–Св14, Св51 | Встраиваемый точечный | в ГКЛ, корпус ≤ 70 мм | 4 | 6 | 24 | 500 | 3000 | 90 | — | 44 | — | L4, L17 | 2, 7 |
| 5 | Св15, Св52 | Настенный светильник над зеркалом, драйвер встроен | над зеркалом, H=1900 | 2 | 8 | 16 | 600 | 3000 | 90 | — | 44 | — | L5, L18 | 2, 7 |
| 6 | Св16 | Потолочный накладной | на потолке, засветка стены | 1 | 10 | 10 | 900 | 3000 | 90 | — | 20 | — | L6 | 3 |
| 7 | Св17–Св22 | Встраиваемый точечный | в ГКЛ, корпус ≤ 70 мм | 6 | 12 | 72 | 1050 | 2700 | 90 | — | 20 | — | L7 | 4 |
| 8 | Св23 | Лента светодиодная 24 В | в карнизе короба, профиль с рассеивателем | 12,3 м | 9,6/м | 118,5 | 900/м | 2700 | 90 | — | 20 | да | L8 | 4 |
| 9 | Св26–Св29, Св53, Св54 | Встраиваемый точечный | в ГКЛ, корпус ≤ 70 мм | 6 | 7 | 42 | 600 | 3000 | 90 | — | 20 | — | L10 | 5, 8 |
| 10 | Св30 | Лента светодиодная 24 В | в коробе, профиль с рассеивателем, датчик движения | 1,8 м | 4,8/м | 8,6 | 150/м | 2700 | 90 | — | 20 | нет | L11 | 5 |
| 11 | Св31–Св40 | Встраиваемый точечный | в ГКЛ, корпус ≤ 70 мм | 10 | 12 | 120 | 1000 | 3000 | 90 | — | 20 | да | L12 | 6 |
| 12 | Св41 | Лента светодиодная 24 В | в карнизе короба, профиль с рассеивателем | 22,1 м | 9,6/м | 211,8 | 900/м | 2700 | 90 | — | 20 | да | L13 | 6 |
| 13 | Св42, Св43, Св44 | Подвесной | подвес, низ H=1450 | 3 | 9 | 27 | 800 | 3000 | 90 | — | 20 | да | L14 | 6 |
| 14 | Св45–Св48 | Встраиваемый точечный | в ГКЛ, корпус ≤ 70 мм | 4 | 10 | 40 | 900 | 3000 | 90 | — | 20 | да | L15 | 6 |
| 15 | Св49 | Линейный настенный | под верхними шкафами, H=1440 | 1 | 18 | 18 | 1500 | 3000 | 90 | — | 20 | да | L16 | 6 |
| 16 | Св50 | Встраиваемый точечный | в ГКЛ, корпус ≤ 70 мм | 1 | 7 | 7 | 600 | 3000 | 90 | — | 44 | — | L17 | 7 |
| | | **Итого** | | **50 шт + 51,7 м** | | **983,7** | | | | | | | | |

## Слои света по помещениям

| Пом. | Помещение | Слои света и группы включения (марки светильников) | Тц, К | Ra | Σ P, Вт | Сцен. |
|---|---|---|---|---|---|---|
| 1 | Спальня 1 | общий — L1 (Св1–Св8); рабочий — L3 (Св10, Св11); акцентный — L2 (Св9) | 2700 | 90 | 256,8 | 2 |
| 2 | Ванная | общий — L4 (Св12–Св14); рабочий — L5 (Св15) | 3000 | 90 | 26 | — |
| 3 | Гардеробная | общий — L6 (Св16) | 3000 | 90 | 10 | — |
| 4 | Спальня 2 | общий — L7 (Св17–Св22); рабочий — L9 (Св24, Св25); акцентный — L8 (Св23) | 2700 | 90 | 202,5 | 1 |
| 5 | Прихожая | общий — L10 (Св26–Св29); ночной — L11 (Св30) | 2700 / 3000 | 90 | 36,6 | — |
| 6 | Кухня-гостиная | общий — L12 (Св31–Св40), L14 (Св42, Св43, Св44), L15 (Св45–Св48); рабочий — L16 (Св49); акцентный — L13 (Св41) | 2700 / 3000 | 90 | 416,8 | 4 |
| 7 | Санузел 2 | общий — L17 (Св50, Св51); рабочий — L18 (Св52) | 3000 | 90 | 21 | — |
| 8 | Коридор | общий — L10 (Св53, Св54) | 3000 | 90 | 14 | — |

## LED-ленты, линейные светильники и блоки питания

| Марка | Пом. | L, м | U, В | Вт/м | Σ P, Вт | БП | P БП, Вт | Загр., % | Питание | Доступ к БП |
|---|---|---|---|---|---|---|---|---|---|---|
| Св9 | 1 | 15,5 | 24 | 9,6 | 148,8 | БП1 | 200 | 74 | с двух концов | люк 300×300 в коробе У1 у входа |
| Св23 | 4 | 12,3 | 24 | 9,6 | 118,5 | БП2 | 200 | 59 | с двух концов | люк 300×300 в коробе У1 у окна |
| Св30 | 5 | 1,8 | 24 | 4,8 | 8,6 | БП3 | 20 | 43 | с одного конца | в шкафу M_13, верхняя полка |
| Св41 | 6 | 22,1 | 24 | 9,6 | 211,8 | БП4 | 300 | 71 | с двух концов | люк 300×300 в коробе У1 у входа |
| Св49 | 6 | 3 | 24 | — | 18 | БП5 | 60 | 30 | встроенный ввод | в пенале M_19, верх, съёмная панель |

## Сценарии освещения

| Пом. | Сценарий | Группы и уровни, % | Чем включается |
|---|---|---|---|
| 1 | Вечер | L1 споты — 0; L2 подсветка короба — 100; L3 бра — 100 | S1, S2, S3 |
| 1 | Уборка | L1 споты — 100; L2 подсветка короба — 100; L3 бра — 0 | S1, S2, S3 |
| 4 | Вечер | L7 споты — 0; L8 подсветка короба — 100; L9 бра — 100 | S4, S5, S6 |
| 6 | Вечер | L12 споты гостиной — 30; L13 подсветка короба — 100; L14 подвесы над столом — 50; L15 споты кухни — 0; L16 подсветка столешницы — 0 | S10 светорегулятор, S11 светорегулятор |
| 6 | Ужин | L12 споты гостиной — 0; L13 подсветка короба — 60; L14 подвесы над столом — 100; L15 споты кухни — 0; L16 подсветка столешницы — 30 | S10 светорегулятор, S11 светорегулятор, S12 светорегулятор |
| 6 | Кино | L12 споты гостиной — 0; L13 подсветка короба — 20; L14 подвесы над столом — 0; L15 споты кухни — 0; L16 подсветка столешницы — 0 | S10 светорегулятор |
| 6 | Готовка | L12 споты гостиной — 50; L13 подсветка короба — 0; L14 подвесы над столом — 0; L15 споты кухни — 100; L16 подсветка столешницы — 100 | S10 светорегулятор, S11 светорегулятор, S12 светорегулятор |
| все | Ушёл | все группы — 0 (свет выключен) | выключатели помещений |

## Слои света

общий — равномерный свет помещения, по норме освещённости

рабочий — местный свет задачи: столешница, зеркало, чтение у кровати

акцентный — подсветка потолка, стен и ниш; не входит в поток общего света

ночной — путь спальня → санузел: не выше 2700 K, малая яркость, датчик движения

## Примечания

1. Позиции и марки Св — те же, что на плане освещения (лист 24) и в ведомости светильников (лист «Ведомость электроточек и изделий»); группы L — по плану выключателей (лист 26).
2. Модели светильников не назначены: подбор по графам спецификации — поток, Тц, Ra, угол, IP и диммирование не хуже указанных, мощность не больше; встраиваемые — под глубину короба (графа «Установка»). IP 20 — сухие помещения.
3. Длина LED-ленты в карнизе — по линии карниза плана потолков (лист 20); Σ P = Вт/м × длина. Блок питания загружен не больше чем на 80 %; лента 24 В длиннее 10 м питается с двух концов; доступ к блоку питания — люк ревизии 300×300 мм или место, указанное в таблице.
4. Сценарии: уровень — доля максимальной яркости группы, %; 0 — группа выключена. Уровень ниже 100 % — только у групп на светорегуляторе (задний фронт, TE) с диммируемыми драйверами и блоками питания.
5. Мощность и поток — по паспортам принятых изделий, Σ P — установленная мощность освещения. Оценка освещённости — на плане освещения; это не светотехнический расчёт.

| | | | | | |
|---|---|---|---|---|---|
| | | | | | Проект: Трёхкомнатная квартира |
| | Лист | № док. | Подпись | Дата | |
| Дизайнер | Кырлан А.С. | | | 05.10.26 | Спецификация светильников и сценарии освещения |
| | | | | | Стадия: П; Лист: 25; Листов: 89 |

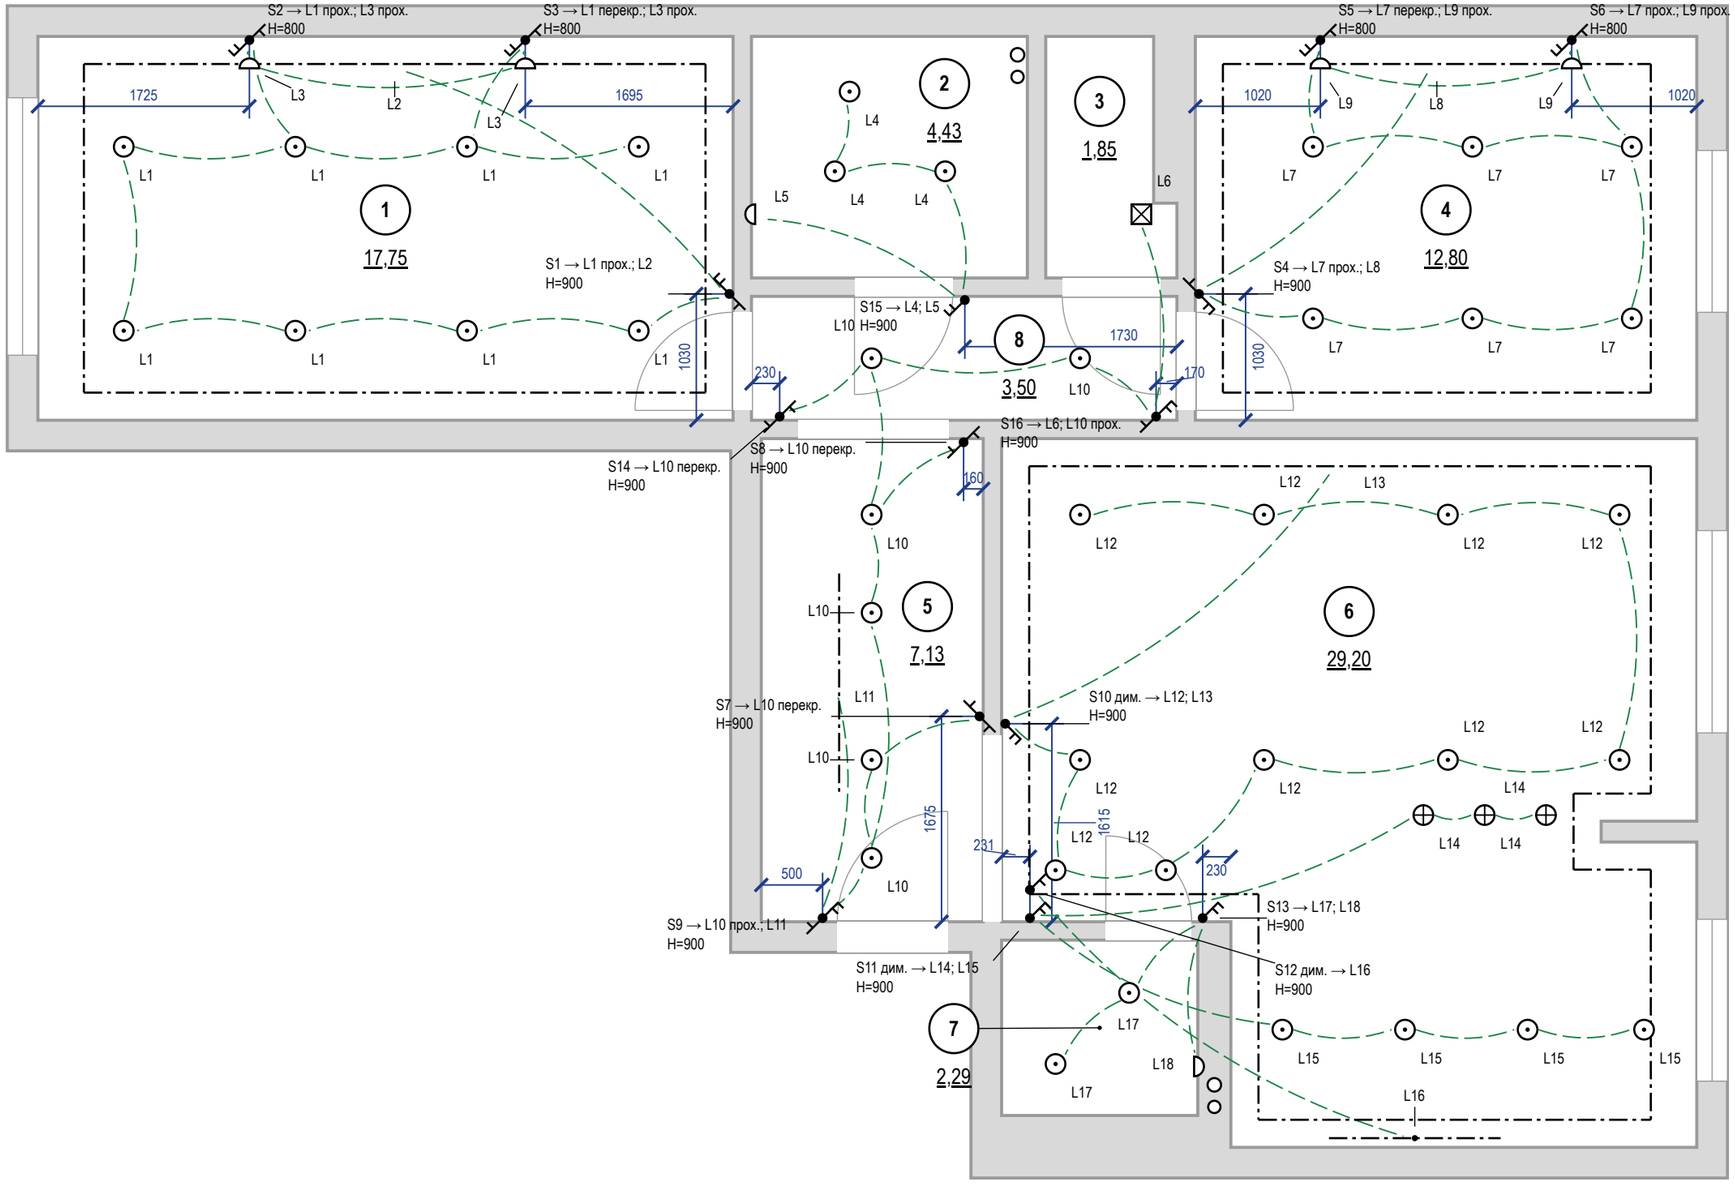


## Примечания

1. За отметку 0,000 принят уровень чистого пола. Высоты H — от чистого пола до оси изделия; привязки — от чистовой грани стены до оси механизма (у рамки на несколько постов — до оси рамки).
2. Высота установки, не указанная на плане: выключатели — 900 мм от чистого пола, со стороны дверной ручки (ПУЭ 7.1.51).
3. Линии связи показывают, какой выключатель какую группу L включает; это не трасса кабеля. Трасса — принципиальная, фактическую зафиксировать исполнительной схемой.
4. Группы из нескольких мест (L1 — S1, S2, S3; L3 — S2, S3; L7 — S4, S5, S6; L9 — S5, S6; L10 — S7, S8, S9, S14, S16): на крайних местах — проходные клавиши, на промежуточных — перекрёстные; механизмы — в ведомости изделий.
5. Светорегулятор — по заднему фронту (для LED-драйверов), совместимость с драйверами проверить до закупки.
6. Розеточные и мокрые линии — через УЗО или дифавтомат с током утечки не более 30 мА (ПУЭ 7.1.79); в санузле выполнить ДСУП (ПУЭ 7.1.87–7.1.88).
7. Кабель — медный, исполнение нг(A)-LS (ГОСТ 31565-2012); скрытая прокладка только горизонтально и вертикально, фактические трассы зафиксировать исполнительной схемой до закрытия отделкой.
8. Расчёт нагрузок, токов КЗ, селективности и сечений — по проекту ЭОМ организации с допуском СРО; лист задаёт состав, расположение и группы.
9. Расшифровка клавиш и ведомость изделий — лист «Ведомость электроточек и изделий».

| | | | | | |
|---|---|---|---|---|---|
| | | | | | Проект: Трёхкомнатная квартира |
| | Лист | № док. | Подпись | Дата | Управление светильниками |
| Дизайнер | Кырлан А.С. | | | 05.10.26 | |

| Стадия | Лист | Листов |
|---|---|---|
| П | 26 | 89 |

выпуск 05.10.2026 № 6a37468da7 · стр. 26 из 89

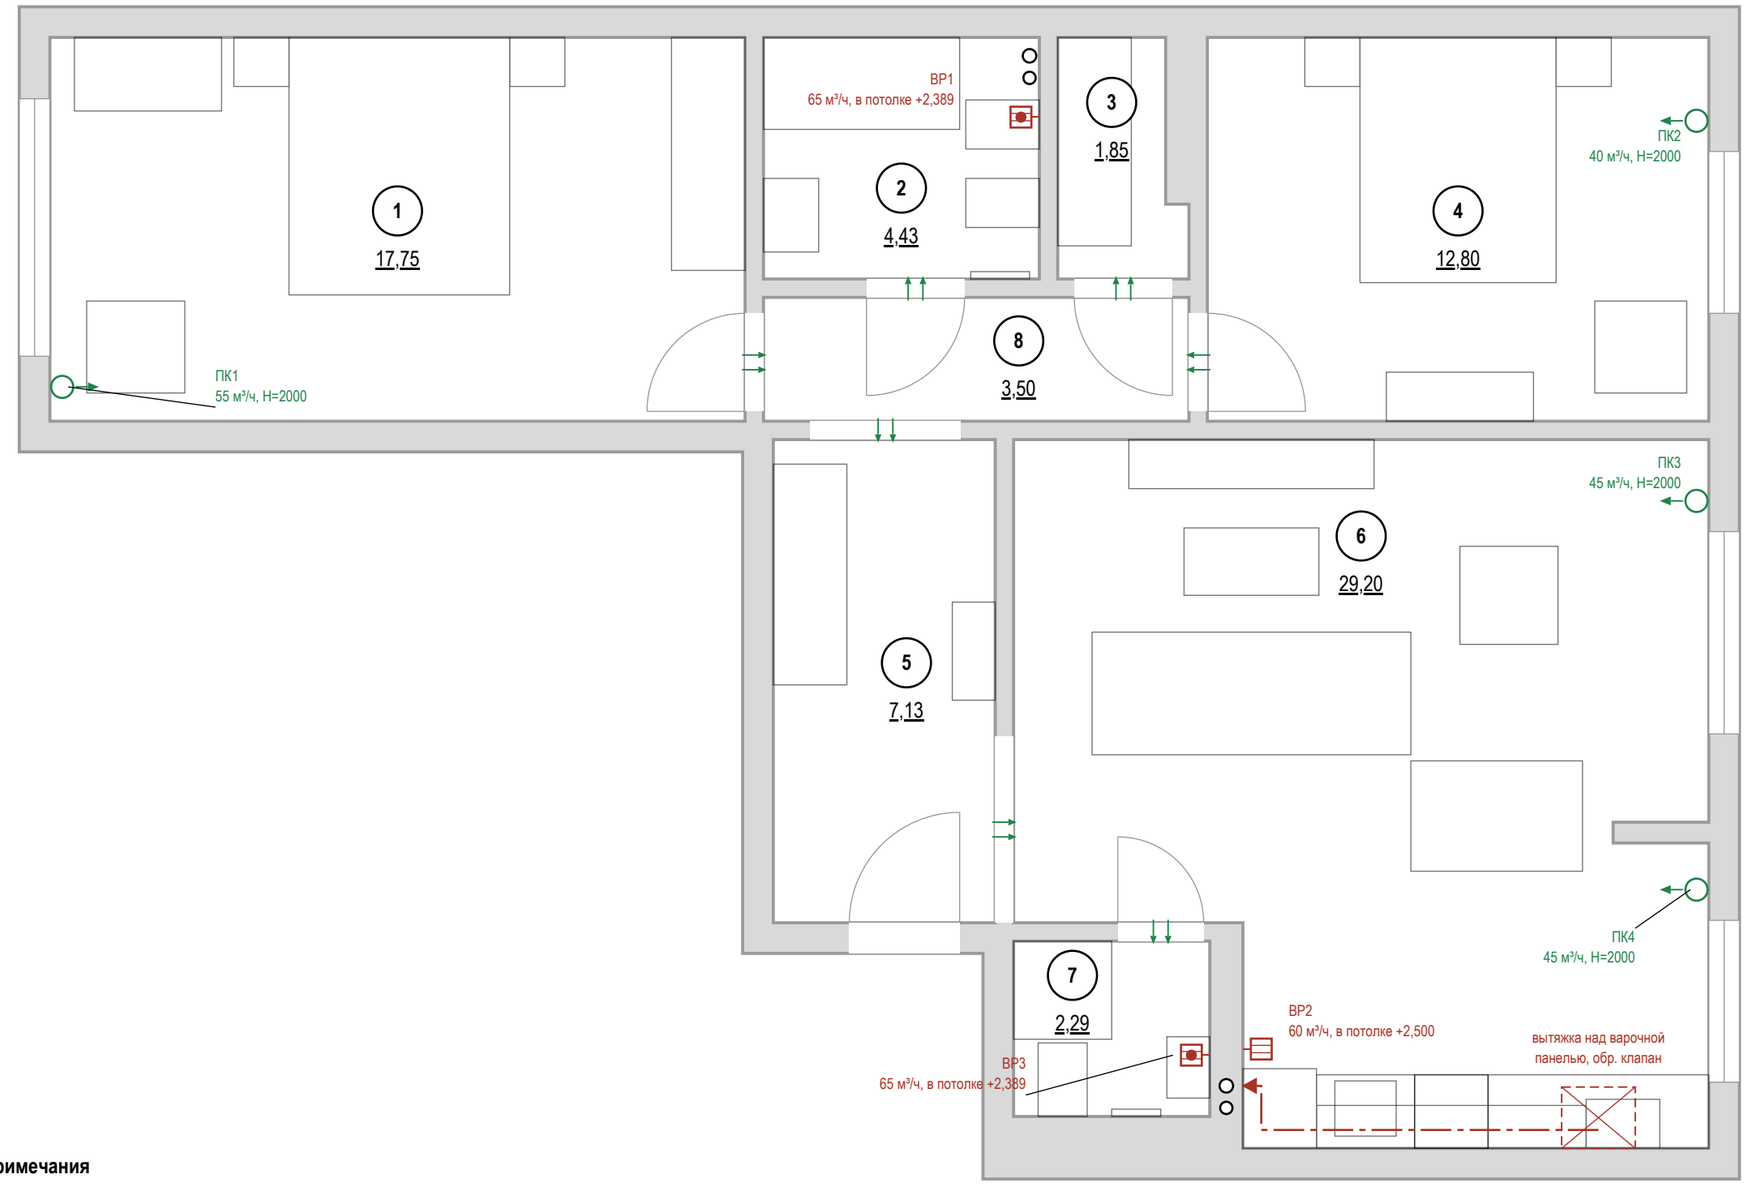


## Условные обозначения

- стояк: К1 — канализация, В1 — ХВС, Т3 — ГВС
- номер помещения, площадь м²
- вытяжная решётка в подшивном потолке, воздуховод за потолком до канала
- вентилятор с обратным клапаном в подшивном потолке, воздуховод за потолком до канала
- приточный клапан (КИВ) в наружной стене: марка, расход, Н центра
- переток: зазор под полотном или переточная решётка
- кухонная вытяжка над варочной панелью
- воздуховод кухонной вытяжки в коробе под потолком
- отдельный вход воздуховода в вентканал, обратный клапан

## Воздухообмен, м³/ч

| № | Помещение | Выт. норма | Выт. проект | Прит. норма | Прит. проект | Устройства |
|---|---|---|---|---|---|---|
| 1 | Спальня 1 | | | 54 | 55 | ПК1 |
| 2 | Ванная | 50 | 65 | | | ВР1 |
| 3 | Гардеробная | 1 | | | | переток |
| 4 | Спальня 2 | | | 39 | 40 | ПК2 |
| 6 | Кухня-гостиная | 60 | 60 | 88 | 90 | ВР2, ПК3, ПК4 |
| 7 | Санузел 2 | 50 | 65 | | | ВР3 |
| | **Итого** | **161** | **190** | **181** | **185** | |

Воздухообмен квартиры — по большей из сумм притока и вытяжки: норма 181 м³/ч, проект 190 м³/ч.
Вытяжка не меньше притока — баланс сведён.

**Привязки — до обмера**
Вентканалы в исходных данных не заданы: решётки и вход вытяжки показаны у стояков К1 (вентблок у мокрой зоны). До черновых работ — обмер каналов и проверка тяги; лист перевыпустить по факту.

## Примечания

1. Расчёт систем ОВ и подбор оборудования — проектная организация с допуском СРО; лист даёт места, трассы и привязки.
2. Нормы вытяжки — СП 54.13330.2022 (Изм. 1, 2), табл. 7.1: кухня с электроплитой 60 м³/ч, с газовой 100; ванная и совмещённый санузел 50; уборная 25; гардеробная 0,2 ч⁻¹. Приток в жилые — 3 м³/ч на 1 м² (менее 20 м² общей площади на человека), иначе 30 м³/ч на человека.
3. Вентканалы и шахты не сужать, не переносить и не закрывать; вентилятор и кухонная вытяжка — через обратный клапан, без перекрытия естественной тяги.
4. Проектные расходы — не ниже нормы, вытяжка сведена с притоком вентиляторами мокрых помещений. Клапаны — в простенке у окна, центр 2000 мм, не над кроватью, не ближе 300 мм к стоякам отопления; типоразмер — на расход.
5. Под подшивным потолком вытяжка — в потолке, воздуховодом за потолком до канала. Кухонная вытяжка в воздухообмен не включена: воздуховод не менее Ø125 в коробе, вход в канал отдельный.
6. Переток — зазор под полотнами межкомнатных дверей или переточная решётка.
7. Кондиционирование заданием не предусмотрено; при установке трассы фреона и дренажа (не менее 40 мм/м, в К1 через сифон) и питание заложить до черновых работ.
8. Привязки оборудования — по паспортам приобретённых моделей, до черновых работ.

| | | | | | |
|---|---|---|---|---|---|
| | | | | | Проект: Трёхкомнатная квартира |
| | Лист | № док. | Подпись | Дата | |
| Дизайнер | Кырлан А.С. | | | 05.10.26 | План вентиляции |

| Стадия | Лист | Листов |
|---|---|---|
| П | 27 | 89 |

выпуск 05.10.2026 № 6a37468da7 · стр. 27 из 89

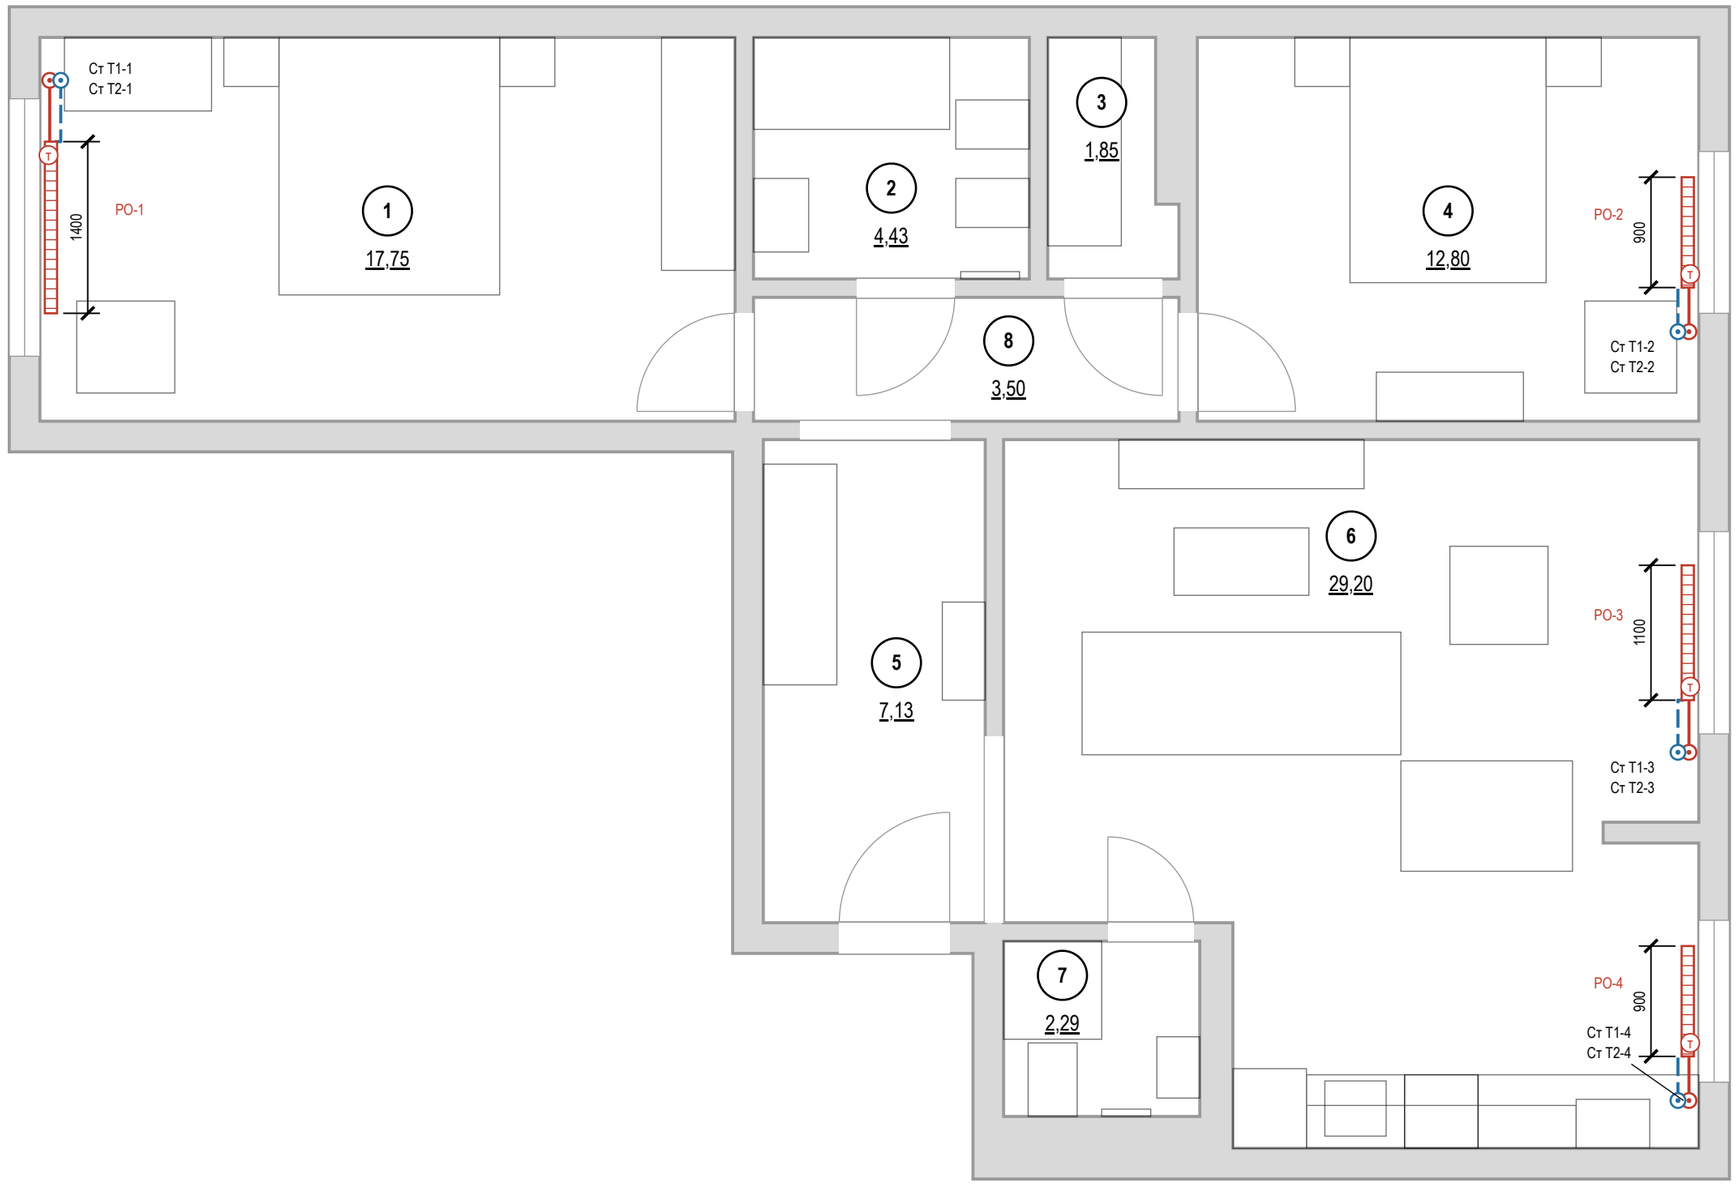


## Условные обозначения

- 1 — номер помещения, площадь м²
- радиатор отопления (марка РО-N, длина по плану)
- клапан с термоголовкой на подаче
- стояк отопления, подающий (Ст Т1-N)
- стояк отопления, обратный (Ст Т2-N)
- Т1 — отопление, подающий трубопровод
- Т2 — отопление, обратный трубопровод

## Ведомость радиаторов

| Марка | Помещение | Тип | Д×В×Г, мм | Низ / стена | Q, Вт |
|---|---|---|---|---|---|
| РО-1 | 1. Спальня 1 | панельный | 1400×600×100 | 120 / 40 | расч. |
| РО-2 | 4. Спальня 2 | панельный | 900×600×100 | 120 / 40 | расч. |
| РО-3 | 6. Кухня-гостиная | панельный | 1100×600×100 | 120 / 40 | расч. |
| РО-4 | 6. Кухня-гостиная | панельный | 900×600×100 | 120 / 40 | расч. |

тип и мощность — по теплотехническому расчёту
Низ — от чистого пола, стена — зазор до задней панели, мм.

**Привязки — до обмера**
Стояки отопления в исходных данных не заданы: показаны у откосов окон, подводки — принципиально. До черновых работ — обмер стояков и паспорта приборов; лист перевыпустить по факту.

## Примечания

1. Расчёт системы отопления, теплопотерь и подбор приборов — проектная организация с допуском СРО; лист даёт места и привязки.
2. Тип, длина и мощность радиаторов — по теплотехническому расчёту; лист задаёт места, зазоры и подключение.
3. Радиаторы — под каждым окном жилых комнат и кухни, центр по оси проёма, длина 0,7 ширины окна (кратно 100); окончательно — по расчёту.
4. Зазоры радиатора: низ не менее 100 мм от чистого пола, верх не менее 100 мм до подоконника, 30–50 мм от стены до задней панели; центр по оси окна с допуском ±20 мм.
5. Радиаторы не закрывать глухими коробами и мебелью; перенос и замена приборов в многоквартирном доме — переустройство, согласование с управляющей организацией (ЖК РФ ст. 25–26); вынос на лоджию запрещён.
6. Трубы отопления через межквартирные стены не прокладывать (СП 51.13330.2011, п. 9.19); через перекрытия и перегородки — в гильзах.
7. Привязки приборов и подводок — по паспортам приобретённых радиаторов и клапанов, до черновых работ.
8. До закрытия отделкой трубопроводы отопления испытать гидростатическим давлением с оформлением акта (СП 73.13330.2016, 7.2–7.3).

| | | | | | |
|---|---|---|---|---|---|
| | | | | | Проект: Трёхкомнатная квартира |
| | Лист | № док. | Подпись | Дата | |
| Дизайнер | Кырлан А.С. | | | 05.10.26 | План отопления |

| Стадия | Лист | Листов |
|---|---|---|
| П | 28 | 89 |

выпуск 05.10.2026 № 6a37468da7 · стр. 28 из 89

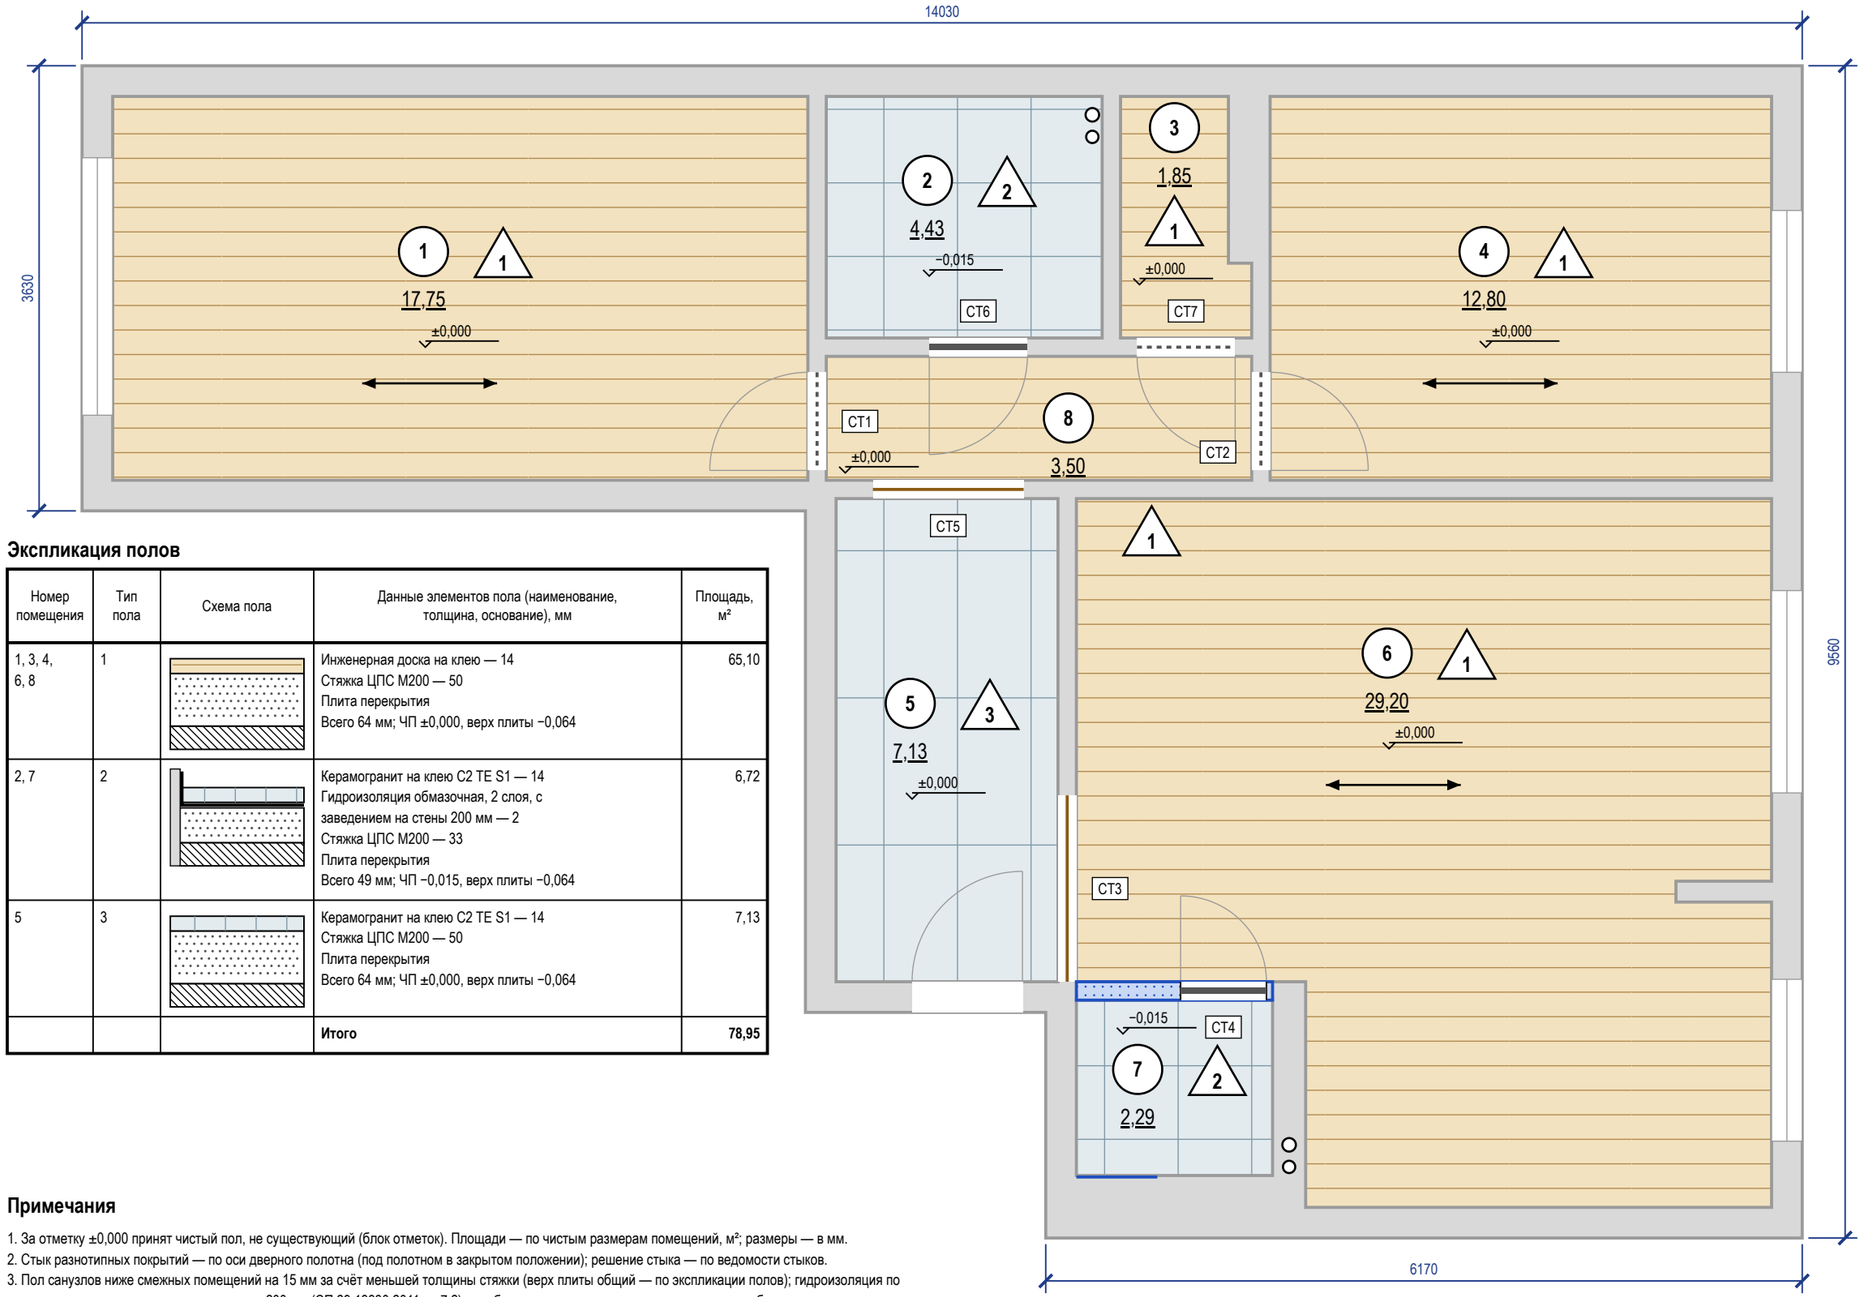


## Экспликация полов

| Номер помещения | Тип пола | Схема пола | Данные элементов пола (наименование, толщина, основание), мм | Площадь, м² |
|---|---|---|---|---|
| 1, 3, 4, 6, 8 | 1 |  | Инженерная доска на клею — 14<br>Стяжка ЦПС М200 — 50<br>Плита перекрытия<br>Всего 64 мм; ЧП ±0,000, верх плиты −0,064 | 65,10 |
| 2, 7 | 2 |  | Керамогранит на клею C2 TE S1 — 14<br>Гидроизоляция обмазочная, 2 слоя, с заведением на стены 200 мм — 2<br>Стяжка ЦПС М200 — 33<br>Плита перекрытия<br>Всего 49 мм; ЧП −0,015, верх плиты −0,064 | 6,72 |
| 5 | 3 |  | Керамогранит на клею C2 TE S1 — 14<br>Стяжка ЦПС М200 — 50<br>Плита перекрытия<br>Всего 64 мм; ЧП ±0,000, верх плиты −0,064 | 7,13 |
| | | | **Итого** | **78,95** |

## Спецификация плинтусов

| Наименование | Помещения | Длина, м (с запасом) |
|---|---|---|
| Плинтус МДФ под покраску 80×16, крепление к стене, окраска в цвет Farrow & Ball No. 241 | 1, 3, 4, 5, 6, 8 | 78 |

## Отметки по высоте

| | |
|---|---|
| **±0,000** | чистый пол пом. 1, 3–6, 8; отсчёт высот |
| **−0,015** | чистый пол пом. 2, 7, ниже на 15 мм |
| **−0,064** | верх плиты — расчёт, не замер |
| **сущ. пол** | снимается до плиты; не замерен |

## Примечания

1. За отметку ±0,000 принят чистый пол, не существующий (блок отметок). Площади — по чистым размерам помещений, м²; размеры — в мм.
2. Стык разнотипных покрытий — по оси дверного полотна (под полотном в закрытом положении); решение стыка — по ведомости стыков.
3. Пол санузлов ниже смежных помещений на 15 мм за счёт меньшей толщины стяжки (верх плиты общий — по экспликации полов); гидроизоляция по стяжке с заведением на стены не менее 200 мм (СП 29.13330.2011, п. 7.2), до облицовки — тест проливом и акт скрытых работ.
4. Трубопроводы в конструкции пола не прокладываются: пирог пола 49–64 мм не вмещает выпуски канализации с уклоном — выпуски К1 ведутся по стенам над чистым полом в коробах (лист 15).
5. Звукоизоляционный слой под стяжкой проектом не предусмотрен (стяжка по плите): приведённый уровень ударного шума перекрытия с полом Lnw не более 60 дБ (СП 51.13330.2011, табл. 2) подтвердить по данным дома; при превышении — плавающая стяжка по звукоизоляции с демпферной лентой по контуру и у стояков, пирог пересчитать.
6. Штучные покрытия (инженерная доска): направление — по стрелке; влажность основания по СМ не более 2,0 % (по ТУ изготовителя).
7. Ровность основания — просвет под 2-метровой рейкой не более 2 мм: пом. 1, 3, 4, 6, 8 (инженерная доска), пом. 2, 5, 7 (керамогранит); проверить до укладки покрытия (СП 71.13330.2017, табл. 8.5).
8. Сетка на плитке — условная, в размер формата; точка старта и раскладка — по листу раскладки плитки.
9. Пироги полов — по экспликации полов: слои сверху вниз, толщины в мм; гидроизоляция мокрых зон — в пироге и в ведомости отделки; схема пола — без масштаба.

| | | | | | |
|---|---|---|---|---|---|
| | | | | | Проект: Трёхкомнатная квартира |
| | Лист | № док. | Подпись | Дата | План покрытий пола |
| Дизайнер | Кырлан А.С. | | | 05.10.26 | Стадия: П; Лист: 29; Листов: 89 |

выпуск 05.10.2026 № 6a37468da7 · стр. 29 из 89

**Фрагмент 1. Ванная (пом. 2). Пол 600×600, шов 2 мм, М 1:20**

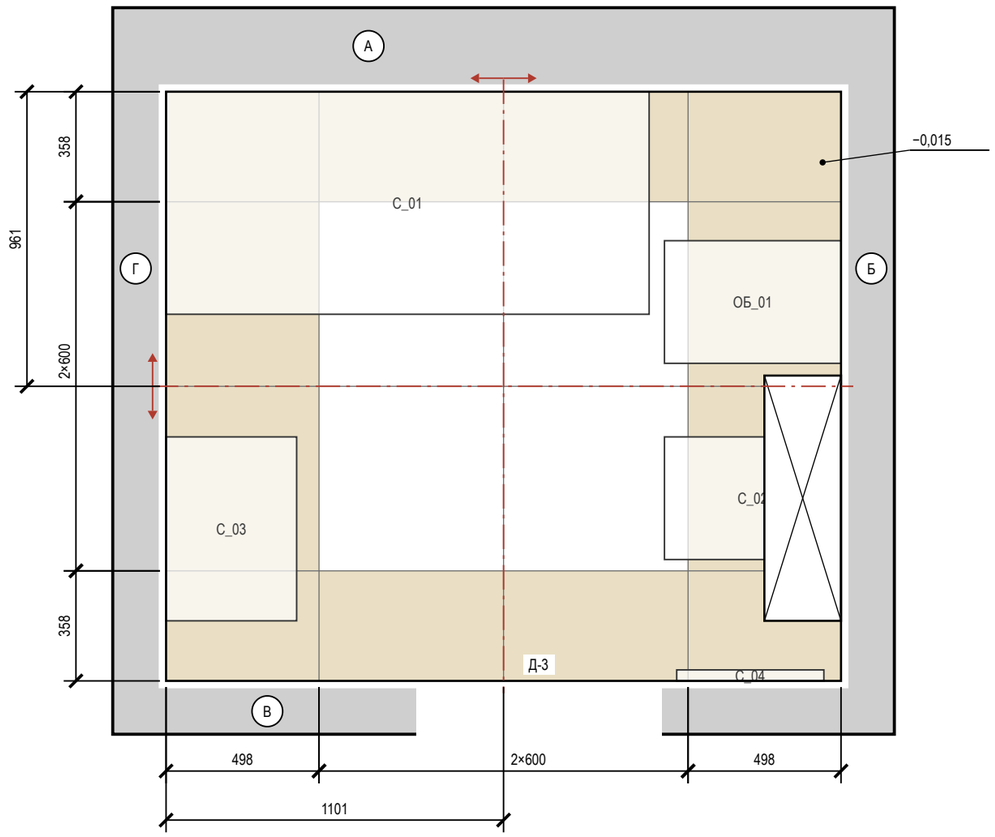


**Фрагмент 2. Санузел 2 (пом. 7). Пол 600×600, шов 2 мм, М 1:20**

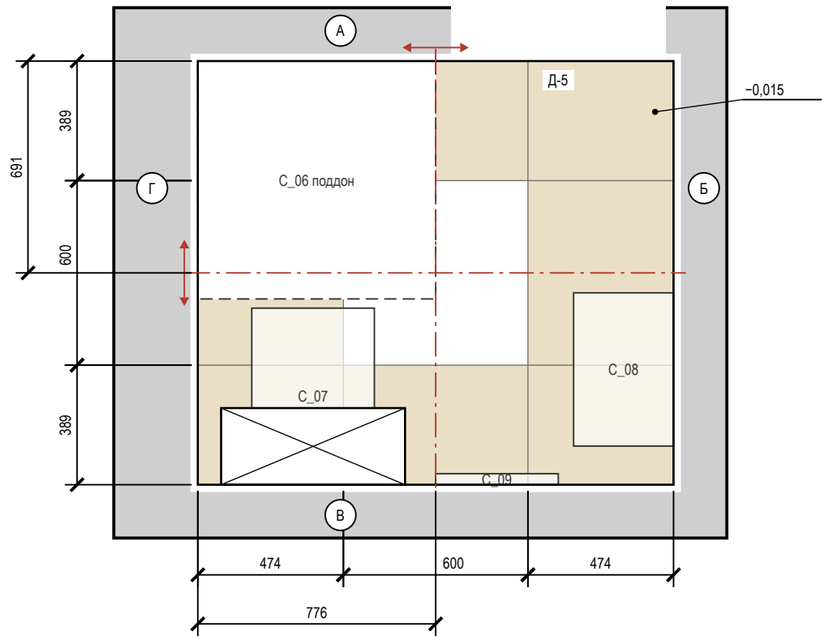


## Примечания

1. Раскладка от чистовых размеров: стены санузлов теряют 10 + 5 + 9 = 24 мм на сторону (штукатурка, клей, плитка); подрезки — чистые, без шва.
2. Старт — от центра помещения (штрихпунктир, стрелки направление укладки); размер старта — от чистовых стен Г и А.
3. Раскладка пола «Прихожая» и фартука «Кухня-гостиная» на листе «Раскладка плитки. Прихожая. Фартук кухни».
4. Калибр партии не задан — до укладки замерить (рабочий размер W, ГОСТ 13996-2019) и пересчитать подрезки.
5. Количество: целые по раскладке + по одной на подрезку, запас 10 %; один артикул — одна партия и тон. Исключены поддон, короб, проёмы и места за коробом; S — по чистым граням: стены нетто = зона облицовки по ведомости отделки − место за коробом инсталляции 1,68 м² (плитку за коробом не кладут), короб — отдельной строкой.
6. Клей C2 TE S1 Ceresit CM 17; C2 TE S1 (ГОСТ Р 56387-2018), затирка CG2WA Mapei Ultracolor Plus 132; CG2WA; расход — по ТУ выбранной марки.
7. Гидроизоляция: пол и стены 200 мм от ЧП; над ванной до 2000 и 300 мм за борт, у душа — до 2000 и 500 мм за поддон (см. развёртки); акт скрытых работ, пролив 24 ч.
8. Швы пола совмещены со швами стены А; по периметру демпферная лента.
9. Отметка чистого пола −0,015, порог 15 мм; стык с соседним покрытием — по оси полотна двери.

## Ведомость материалов

| Материал | Класс, код | Норма расхода | Кол-во |
|---|---|---|---|
| Затирка | CG2WA Mapei Ultracolor Plus 132 | (a+b)/ab·шов·t·1,6 | 3,1 кг |
| Затирка | CG2WA | (a+b)/ab·шов·t·1,6 | 0,7 кг |
| Клей | C2 TE S1 Ceresit CM 17 | 1,5 кг/м²·мм, слой 5 | 312 кг (13 меш.) |
| Клей | C2 TE S1 | 1,5 кг/м²·мм, слой 5 | 73 кг (3 меш.) |
| Гидроизоляция | обмазочная, 2 слоя: пол, стены по периметру и зоны замачивания | по ТУ | 20,0 м² |
| Демпф. лента | по периметру пола из плитки | | 22,4 м |

## Ведомость плитки

| Помещение, поверхность | Плитка, код | Формат | Шов | S, м² | Целых | Подр. | С запасом |
|---|---|---|---|---|---|---|---|
| Ванная, пол | аналог: керамогранит под травертин | 600×600 | 2 | 4,43 | 4 | 12 | 18 |
| Ванная, стены А–Г | аналог: керамогранит под травертин | 600×1200 | 2 | 17,65 | 10 | 21 | 35 |
| Ванная, короб инсталляции | аналог: керамогранит под травертин | 600×1200 | 2 | 1,76 | 0 | 6 | 7 |
| Санузел 2, пол | аналог: керамогранит под травертин | 600×600 | 2 | 2,29 | 0 | 8 | 9 |
| Санузел 2, стены А–Г | аналог: керамогранит под травертин | 600×1200 | 2 | 12,38 | 5 | 19 | 28 |
| Санузел 2, короб инсталляции | аналог: керамогранит под травертин | 600×1200 | 2 | 1,47 | 1 | 3 | 5 |
| Прихожая, пол | аналог: керамогранит ректифицированный под травертин, матовый | 600×1200 | 2 | 7,13 | 2 | 10 | 14 |
| Кухня-гостиная, фартук (ст. В) | аналог: керамогранит под травертин, матовый | 1200×600 | 2 | 1,87 | 0 | 4 | 5 |
| Итого 600×600 | | | | 6,72 | 4 | 20 | 27 |
| **Итого 600×1200** | | | | **42,26** | **18** | **63** | **94** |

## Условные обозначения

- плитка целая; тонкая линия — шов
- плитка с подрезкой (размер — на цепочке)
- ось старта; стрелки — направление укладки
- сантехприбор: габарит, высота по практике
- поддон душа — плитку пола под ним не кладут
- короб инсталляции: плитка пола — до короба
- отметка чистого пола на полке выноски, м
- (А) обозначение стены А–Г (как на развёртках)

| | | | | | |
|---|---|---|---|---|---|
| | | | | | Проект: Трёхкомнатная квартира |
| | Лист | № док. | Подпись | Дата | |
| Дизайнер | Кырлан А.С. | | | 05.10.26 | Раскладка плитки. Планы полов |
| | | | | | Стадия: П; Лист: 30; Листов: 89 |

**Фрагмент 1. Прихожая (пом. 5). Пол 600×1200, шов 2 мм, М 1:20**

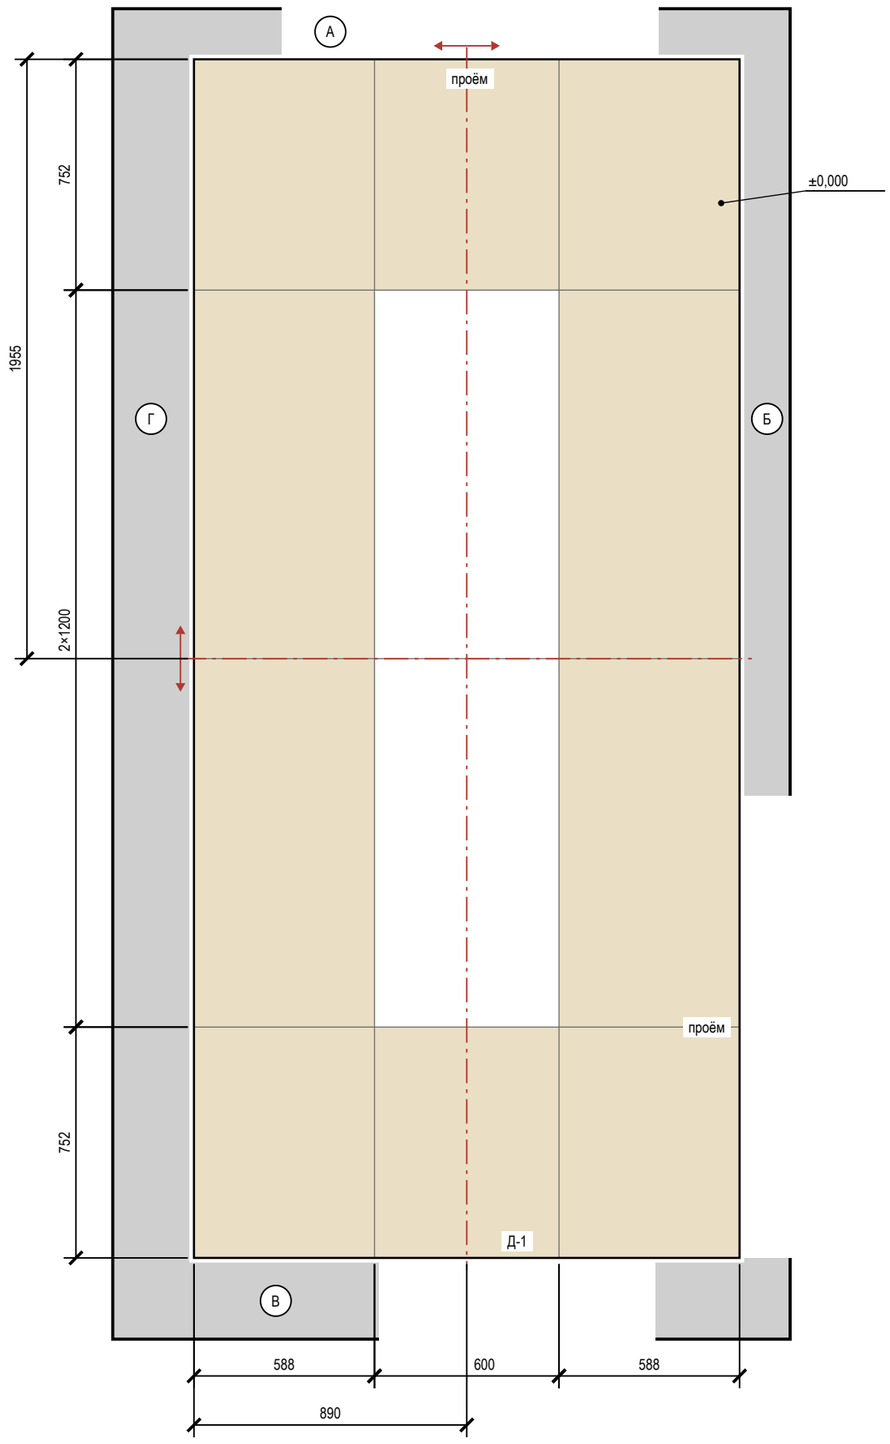


**Фрагмент 2. Кухня-гостиная (пом. 6), фартук, стена В. 1200×600, шов 2 мм, М 1:20**

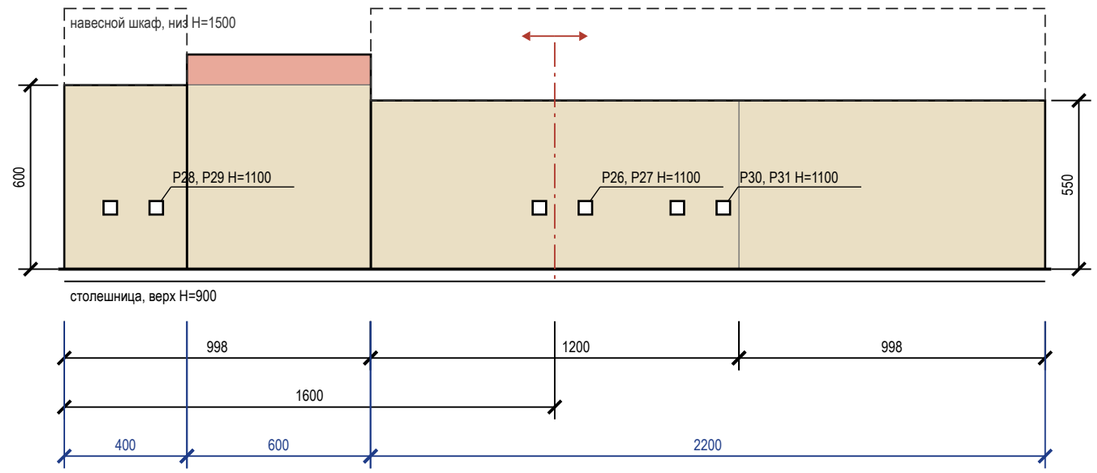


## Условные обозначения

- плитка целая; тонкая линия — шов
- плитка с подрезкой (размер — на цепочке)
- ось старта; стрелки — направление укладки
- электроточка: марка и H — по листам ЭОМ
- столешница (верх)
- навесной шкаф над фартуком
- отметка чистого пола на полке выноски, м
- (А) обозначение стены А–Г (как на развёртках)

## Подсчёт плитки

| Поверхность | Формат | S, м² | Целых | Подр. | С запасом |
|---|---|---|---|---|---|
| Прихожая, пол | 600×1200 | 7,13 | 2 | 10 | 14 |
| Кухня-гостиная, фартук (ст. В) | 1200×600 | 1,87 | 0 | 4 | 5 |

## Сдвиг розеток фартука под раскладку

| Точка (ЭОМ) | Проект: от угла / H | Под раскладку: от угла / H | Сдвиг, мм |
|---|---|---|---|
| P26, P27, P30, P31 | 1700, 1550, 2150, 2000 / 1100 | 1700, 1550, 2150, 2000 / 1175 | H +75 — ось ряда |
| P28, P29 | 300, 150 / 1100 | 300, 150 / 1200 | H +100 — ось ряда |

## Примечания

1. Прихожая: керамогранит 600×1200, длинная сторона — вдоль стен Б и Г, шов 2 мм, прямая раскладка от центра. Стены окрашены: раскладка от чистового контура минус штукатурка и шпаклёвка 15 мм на сторону (принято); подрезки 588 / 752 мм, срез — под плинтус.
2. Прихожая: деформационный зазор по периметру 8–10 мм под плинтусом; в проёмах — стык с соседним покрытием по оси полотна двери. Клей C2 TE S1, затирка CG2WA.
3. Фартук, Кухня-гостиная: 1200×600 горизонтально, шов 2 мм; зоны 2200 мм — 900…1450, 600 мм — 900…1600, 400 мм — 900…1500 (от столешницы до низа навесного шкафа, без шкафа — 700 мм). Старт от центра участка, подрезки 998 мм. Площадь 1,87 м² — как в ведомости отделки.
4. Фартук — после монтажа столешницы, низ на 2–3 мм выше неё, шов со столешницей — санитарный герметик; навесные шкафы — после фартука. Торцы у пенала и стены — профиль или запил 45°.
5. Фартук, Кухня-гостиная: в зоне до отм. 1600 верхний ряд подрезан 98 мм — меньше 1/3 плитки; полоса прикрыта корпусом навесного модуля и на виду не остаётся. Раскладкой не снимается: убрать подрезку можно, только выровняв низ этого модуля с соседними (1450 мм) — решение мебельщика.
6. Розетки из таблицы переносятся до черновой электрики: по высоте — на ось ряда плитки, от вертикального шва крупной плитки — не ближе 60 мм. Привязка — от левого края фартука на развёртке.
7. Клей, затирка и итог по форматам — в ведомостях листа «Раскладка плитки. Планы полов».

| | | | | | |
|---|---|---|---|---|---|
| | | | | | Проект: Трёхкомнатная квартира |
| | Лист | № док. | Подпись | Дата | Раскладка плитки. Прихожая. Фартук кухни |
| Дизайнер | Кырлан А.С. | | | 05.10.26 | |

| Стадия | Лист | Листов |
|---|---|---|
| П | 31 | 89 |

| | | | | | |
|---|---|---|---|---|---|
| | | | | | Проект: Трёхкомнатная квартира |
| | Лист | № док. | Подпись | Дата | |
| Дизайнер | Кырлан А.С. | | | 05.10.26 | Визуализация. Вид сверху |
| | | | | | Стадия: П; Лист: 32; Листов: 89 |

выпуск 05.10.2026 № 6a37468da7 · стр. 32 из 89

| | | | | | | |
|---|---|---|---|---|---|---|
| | | | | | Проект: Трёхкомнатная квартира | |
| | Лист | № док. | Подпись | Дата | | |
| Дизайнер | Кырлан А.С. | | | 05.10.26 | Визуализация | Стадия / Лист / Листов |
| | | | | | | П / 33 / 89 |

выпуск 05.10.2026 № 6a37468da7 · стр. 33 из 89

| | | | | | | |
|---|---|---|---|---|---|---|
| | | | | | Проект: Трёхкомнатная квартира | |
| | Лист | № док. | Подпись | Дата | | |
| Дизайнер | Кырлан А.С. | | | 05.10.26 | Визуализация: Спальня 1 | Стадия / Лист / Листов |
| | | | | | | П / 34 / 89 |

выпуск 05.10.2026 № 6a37468da7 · стр. 34 из 89

| | | | | | | |
|---|---|---|---|---|---|---|
| | | | | | Проект: Трёхкомнатная квартира | |
| | Лист | № док. | Подпись | Дата | | |
| Дизайнер | Кырлан А.С. | | | 05.10.26 | Визуализация: Спальня 1 | Стадия / Лист / Листов |
| | | | | | | П / 35 / 89 |

выпуск 05.10.2026 № 6a37468da7 · стр. 35 из 89

| | | | | | |
|---|---|---|---|---|---|
| | | | | | Проект: Трёхкомнатная квартира |
| | Лист | № док. | Подпись | Дата | |
| Дизайнер | Кырлан А.С. | | | 05.10.26 | Визуализация: Спальня 1 |

| Стадия | Лист | Листов |
|---|---|---|
| П | 36 | 89 |

выпуск 05.10.2026 · 6a37468da7 · стр. 36 из 89

## Развёртка стены А

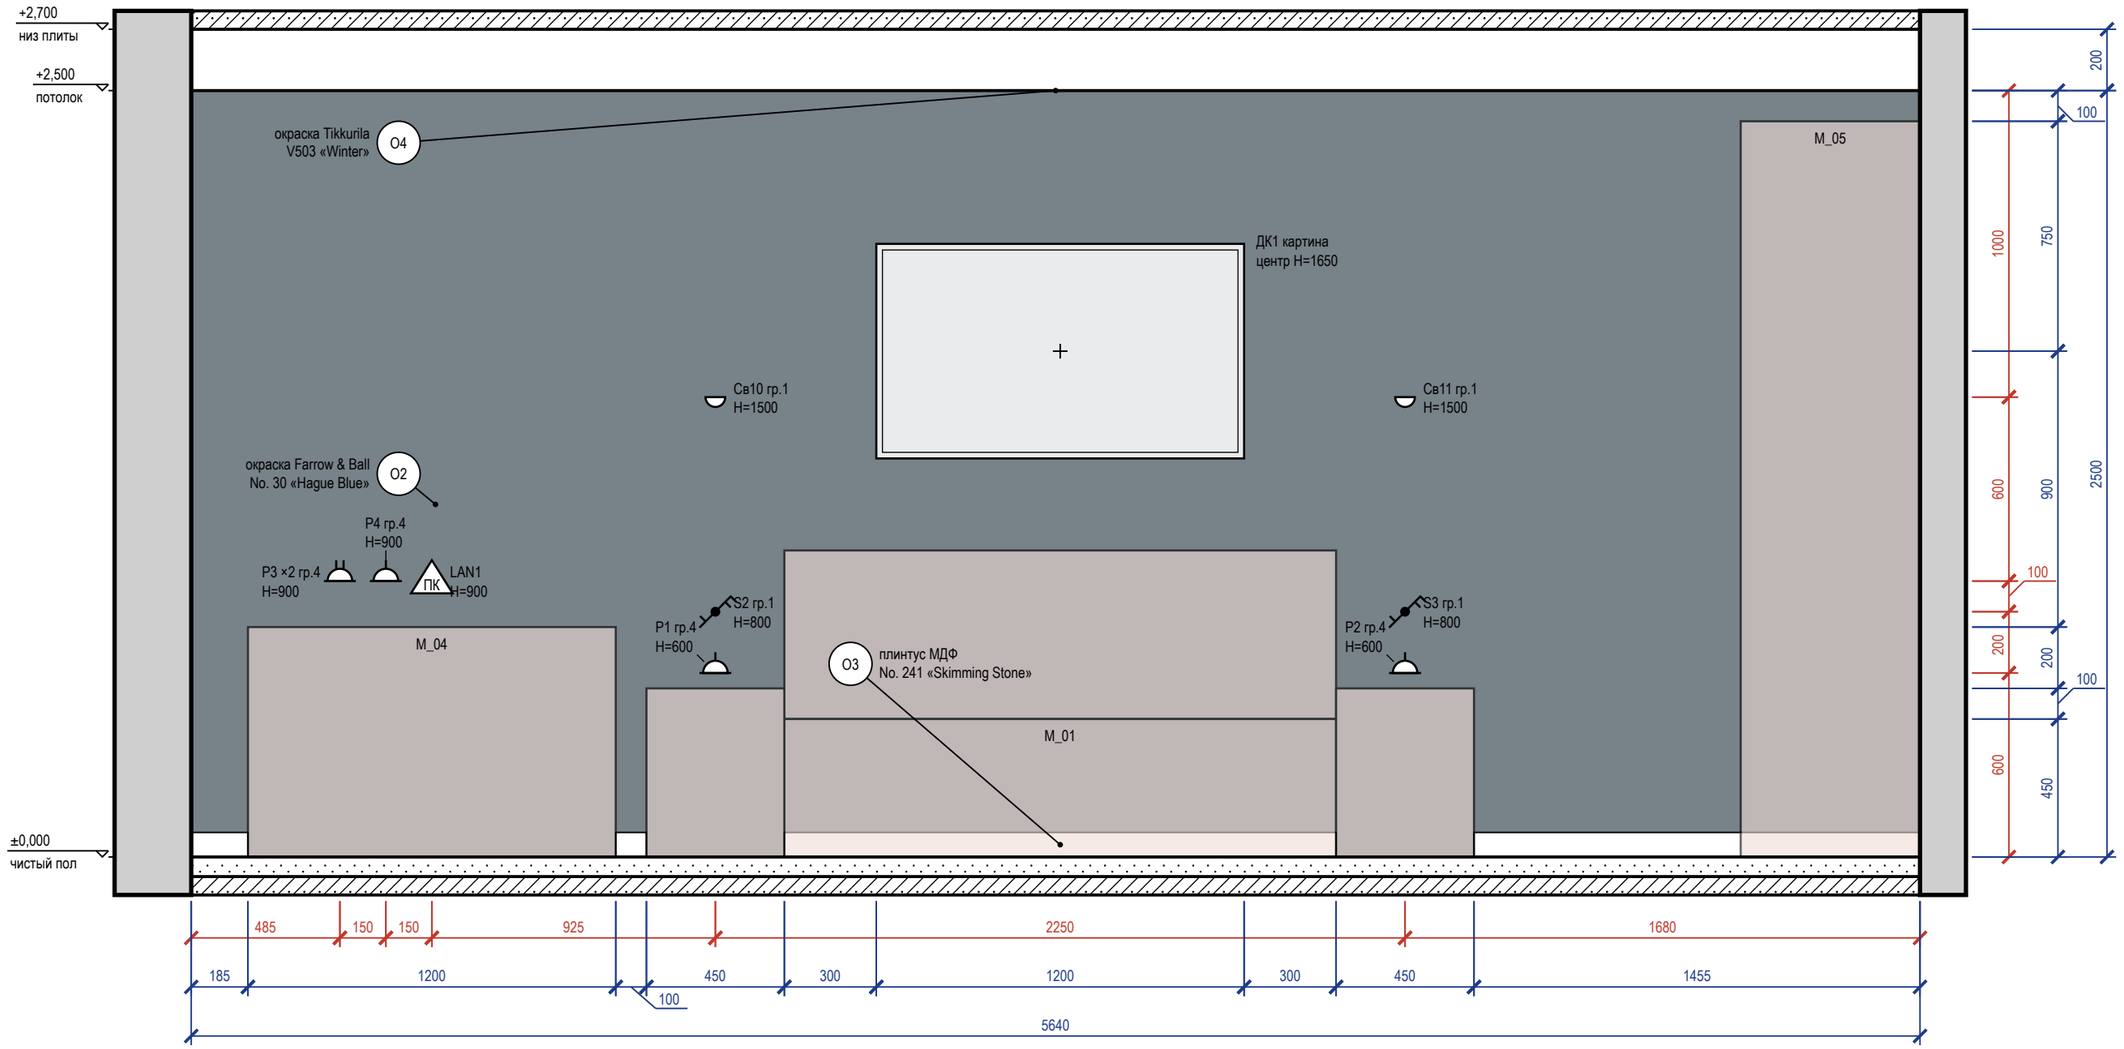


### Схема развёрток (М 1:100)

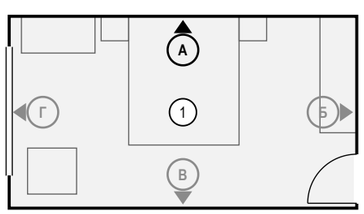


### Ведомость отделки (на листе)

| Марка | Поверхность | Материал, изделие | Цвет, код | Кол. |
|---|---|---|---|---|
| О2 | акцентная стена | окраска, Farrow & Ball Modern Emulsion, матовая, подготовка Q3 | Farrow & Ball No. 30 «Hague Blue» | 14,1 м² |
| О3 | плинтус | плинтус МДФ, h 80 мм, аналог: плинтус МДФ под покраску 80×16 | Farrow & Ball No. 241 «Skimming Stone» | 3,5 м |
| О4 | потолок | окраска, Tikkurila Anti-Reflex 2, глубокоматовая, подготовка Q3 | Tikkurila V503 «Winter» | 17,8 м² |

Визуализация этой стены — лист 35

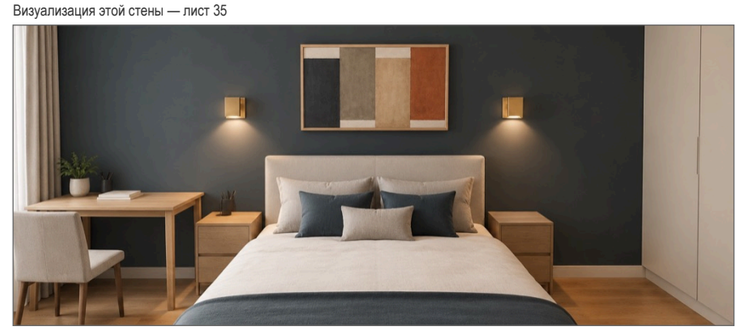

### Примечания

1. Размеры — в мм от чистовых поверхностей стен; условные обозначения и общие указания — лист 2.
2. Картины и зеркала крепить к основанию по паспорту изделия (закладные и анкеры — в перечне скрытых работ); крест — ось центра предмета.
3. Потолок на развёртках — по нижнему уровню У1; другие уровни потолка помещения: У2 +2,600.

| | Лист | № док. | Подпись | Дата |
|---|---|---|---|---|
| Дизайнер | Кырлан А.С. | | | 05.10.26 |

Проект: Трёхкомнатная квартира

Развёртка стены А. Спальня 1 (пом. 1)

| Стадия | Лист | Листов |
|---|---|---|
| П | 37 | 89 |

выпуск 05.10.2026 № 6a37468da7 · стр. 37 из 89

## Развёртка стены Б

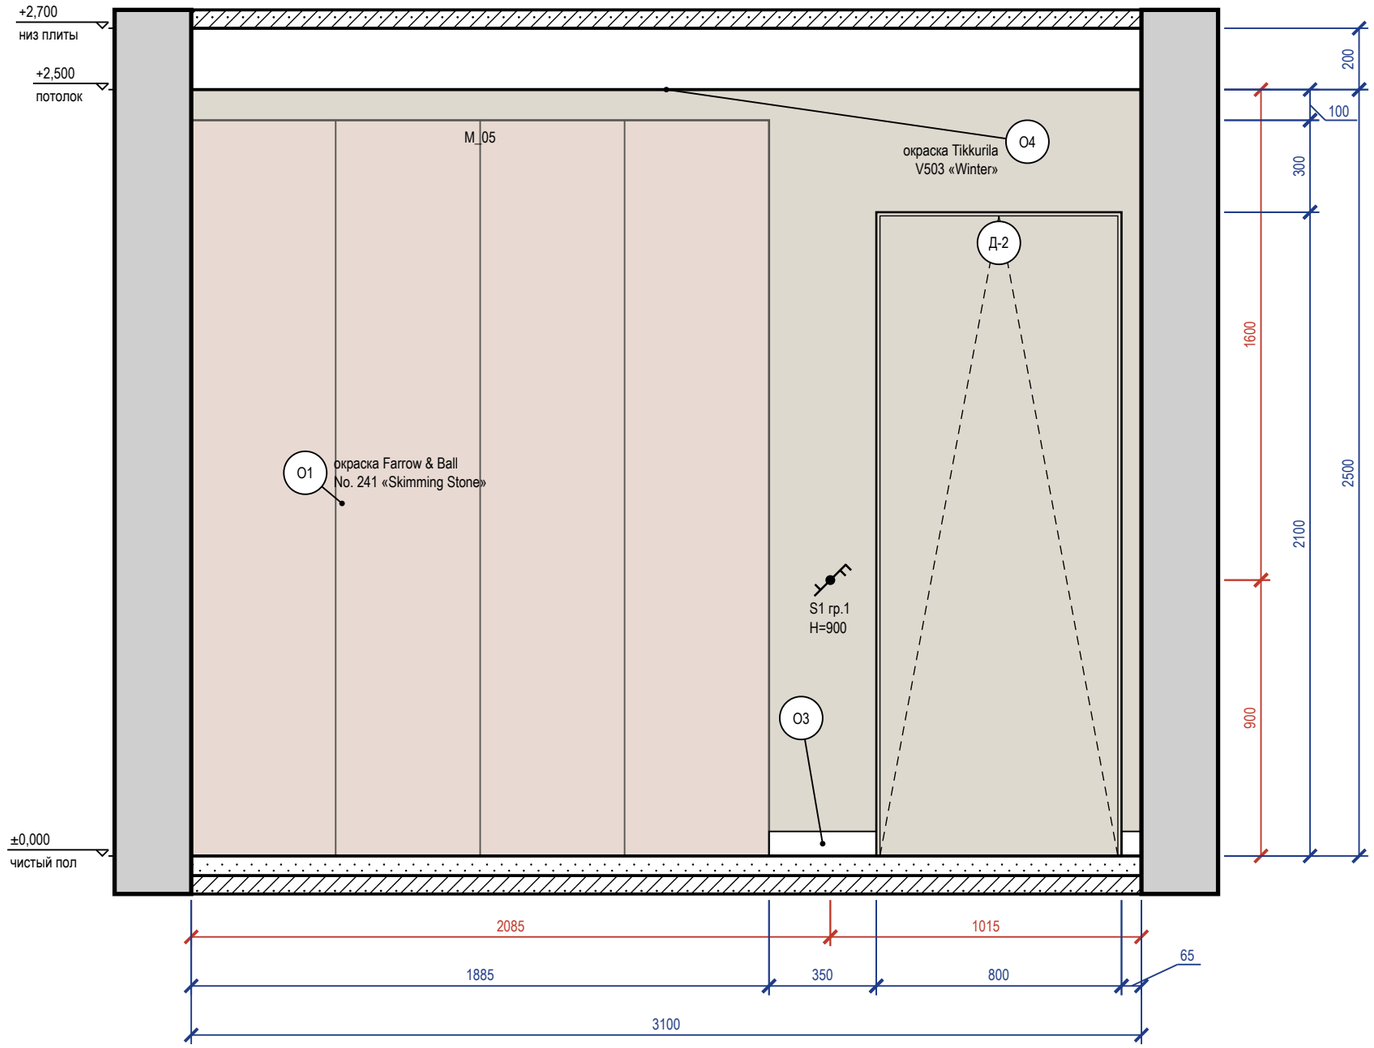


## Схема развёрток (М 1:100)

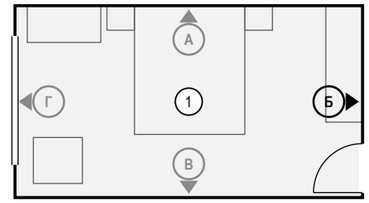


## Ведомость отделки (на листе)

| Марка | Поверхность | Материал, изделие | Цвет, код | Кол. |
|---|---|---|---|---|
| О1 | стены | окраска, Farrow & Ball Modern Emulsion, матовая, подготовка Q3 | Farrow & Ball No. 241 «Skimming Stone» | 6,1 м² |
| О3 | плинтус | плинтус МДФ, h 80 мм, аналог: плинтус МДФ под покраску 80×16 | Farrow & Ball No. 241 «Skimming Stone» | 0,4 м |
| О4 | потолок | окраска, Tikkurila Anti-Reflex 2, глубокоматовая, подготовка Q3 | Tikkurila V503 «Winter» | 17,8 м² |

Визуализация этой стены — лист 36

## Примечания

1. Размеры — в мм от чистовых поверхностей стен; условные обозначения и общие указания — лист 2.
2. Двери скрытого монтажа — полотно в плоскости стены, отделка стены по полотну, плинтус прерывается у короба (узел — на листе узлов).
3. Потолок на развёртках — по нижнему уровню У1; другие уровни потолка помещения: У2 +2,600.

| | | | | | |
|---|---|---|---|---|---|
| | | | | | Проект: Трёхкомнатная квартира |
| | Лист | № док. | Подпись | Дата | |
| Дизайнер | Кырлан А.С. | | | 05.10.26 | Развёртка стены Б. Спальня 1 (пом. 1) |

| Стадия | Лист | Листов |
|---|---|---|
| П | 38 | 89 |

выпуск 05.10.2026 № 6a37468da7 · стр. 38 из 89

## Развёртка стены В

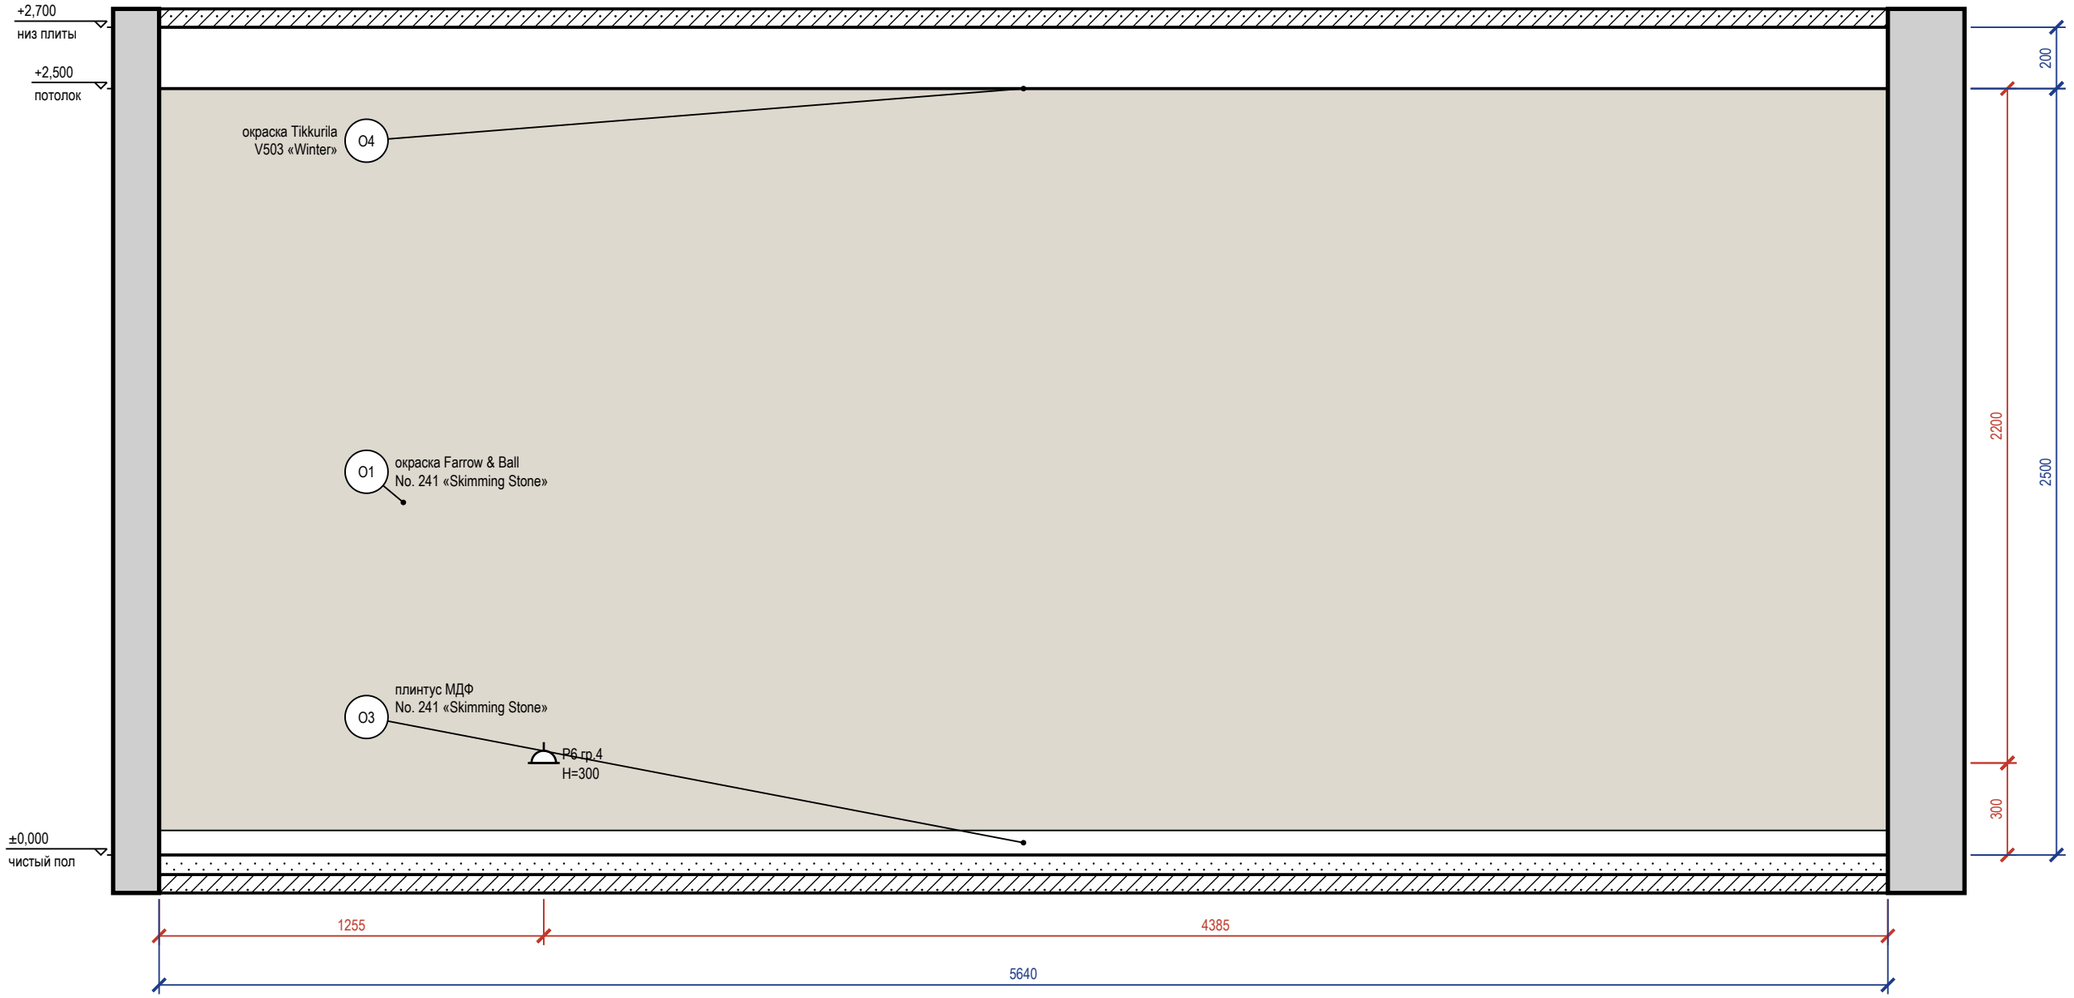


### Схема развёрток (М 1:100)

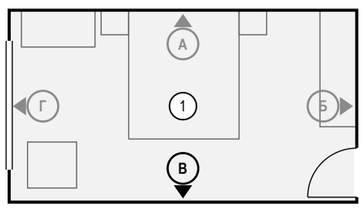


### Ведомость отделки (на листе)

| Марка | Поверхность | Материал, изделие | Цвет, код | Кол. |
|---|---|---|---|---|
| О1 | стены | окраска, Farrow & Ball Modern Emulsion, матовая, подготовка Q3 | Farrow & Ball No. 241 «Skimming Stone» | 14,1 м² |
| О3 | плинтус | плинтус МДФ, h 80 мм, аналог: плинтус МДФ под покраску 80×16 | Farrow & Ball No. 241 «Skimming Stone» | 5,6 м |
| О4 | потолок | окраска, Tikkurila Anti-Reflex 2, глубокоматовая, подготовка Q3 | Tikkurila V503 «Winter» | 17,8 м² |

### Примечания

1. Размеры — в мм от чистовых поверхностей стен; условные обозначения и общие указания — лист 2.
2. Потолок на развёртках — по нижнему уровню У1; другие уровни потолка помещения: У2 +2,600.

| | | | | | |
|---|---|---|---|---|---|
| | | | | | Проект: Трёхкомнатная квартира |
| | Лист | № док. | Подпись | Дата | |
| Дизайнер | Кырлан А.С. | | | 05.10.26 | Развёртка стены В. Спальня 1 (пом. 1) |

| Стадия | Лист | Листов |
|---|---|---|
| П | 39 | 89 |

выпуск 05.10.2026 № 6a37468da7 · стр. 39 из 89

## Развёртка стены Г

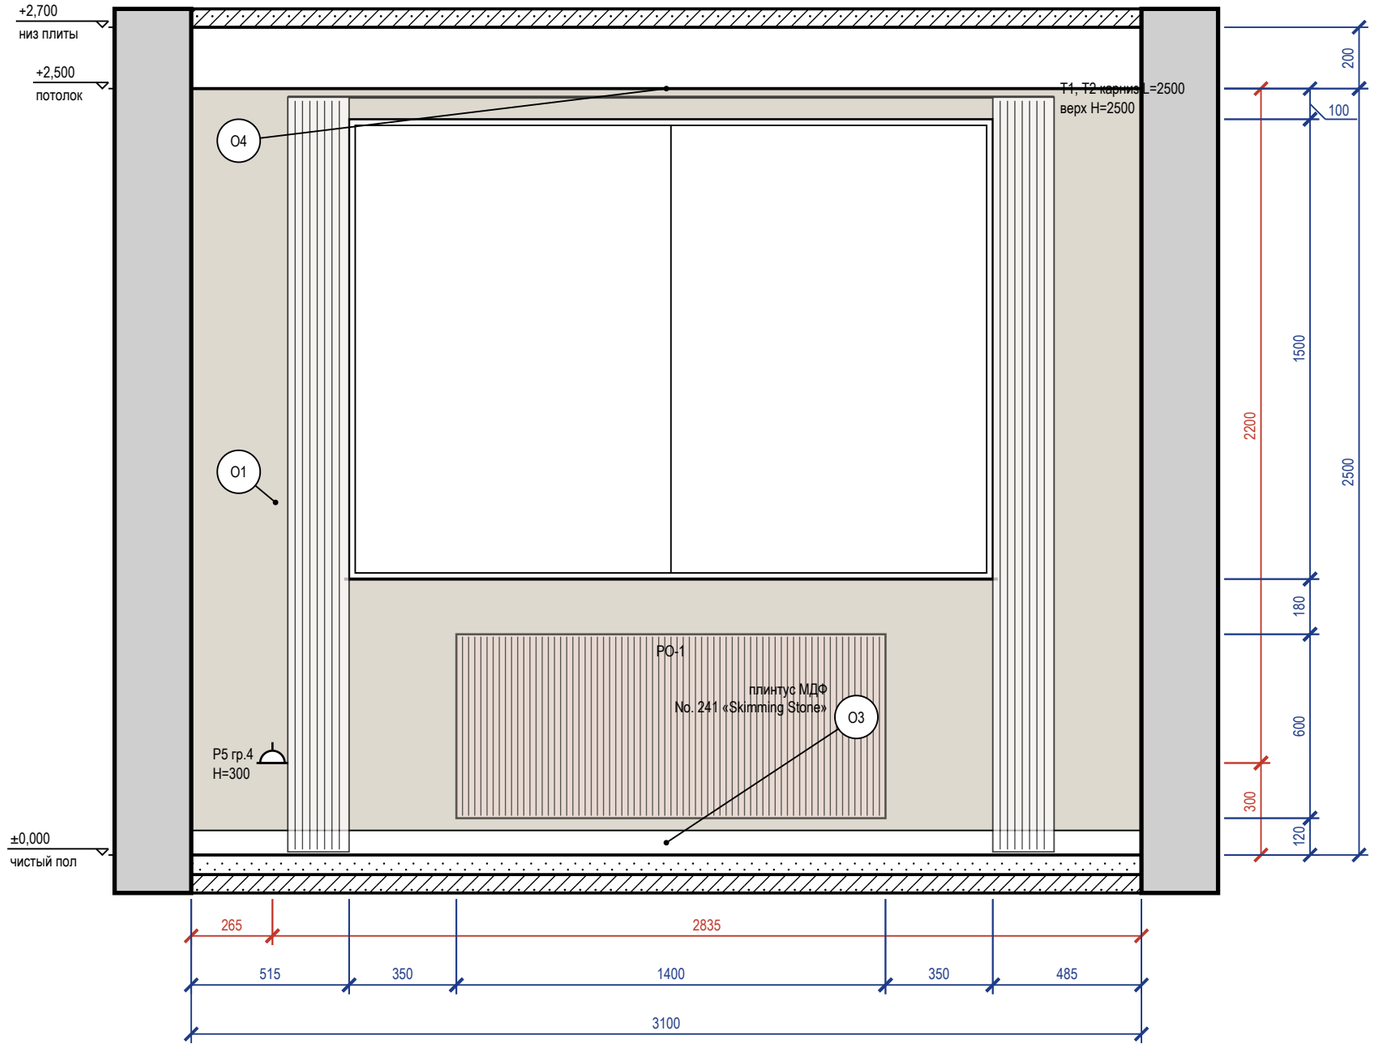


## Схема развёрток (М 1:100)

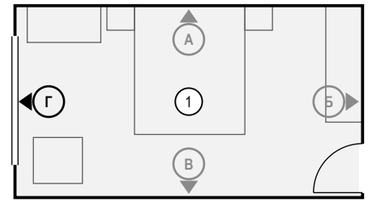


## Ведомость отделки (на листе)

| Марка | Поверхность | Материал, изделие | Цвет, код | Кол. |
|---|---|---|---|---|
| О1 | стены | окраска, Farrow & Ball Modern Emulsion, матовая, подготовка Q3 | Farrow & Ball No. 241 «Skimming Stone» | 4,6 м² |
| О3 | плинтус | плинтус МДФ, h 80 мм, аналог: плинтус МДФ под покраску 80×16 | Farrow & Ball No. 241 «Skimming Stone» | 3,1 м |
| О4 | потолок | окраска, Tikkurila Anti-Reflex 2, глубокоматовая, подготовка Q3 | Tikkurila V503 «Winter» | 17,8 м² |

Визуализация этой стены — лист 34

## Примечания

1. Размеры — в мм от чистовых поверхностей стен; условные обозначения и общие указания — лист 2.
2. Карнизы (шины) — по ведомости текстиля декоратора; длина L и верх H — по развёртке, крепление — до окраски потолка.
3. Потолок на развёртках — по нижнему уровню У1; другие уровни потолка помещения: У2 +2,600.

| | Лист | № док. | Подпись | Дата |
|---|---|---|---|---|
| Дизайнер | Кырлан А.С. | | | 05.10.26 |

Проект: Трёхкомнатная квартира

Развёртка стены Г. Спальня 1 (пом. 1)

| Стадия | Лист | Листов |
|---|---|---|
| П | 40 | 89 |

выпуск 05.10.2026 № 6a37468da7 · стр. 40 из 89

| | | | | | |
|---|---|---|---|---|---|
| | | | | | Проект: Трёхкомнатная квартира |
| | | | | | |
| | Лист | № док. | Подпись | Дата | |
| Дизайнер | Кырлан А.С. | | | 05.10.26 | Визуализация ванной |
| | | | | | |

| Стадия | Лист | Листов |
|---|---|---|
| П | 41 | 89 |

выпуск 05.10.2026 № 6a37468da7 · стр. 41 из 89

| | | | | | |
|---|---|---|---|---|---|
| | | | | | Проект: Трёхкомнатная квартира |
| | Лист | № док. | Подпись | Дата | |
| Дизайнер | Кырлан А.С. | | | 05.10.26 | Визуализация ванной |

| Стадия | Лист | Листов |
|---|---|---|
| П | 42 | 89 |

выпуск 05.10.2026 № 6a37468da7 · стр. 42 из 89

| | | | | | |
|---|---|---|---|---|---|
| | | | | | Проект: Трёхкомнатная квартира |
| | Лист | № док. | Подпись | Дата | |
| Дизайнер | Кырлан А.С. | | | 05.10.26 | Визуализация ванной |

| Стадия | Лист | Листов |
|---|---|---|
| П | 43 | 89 |

выпуск 05.10.2026 № 6a37468da7 · стр. 43 из 89

| | | | | | | |
|---|---|---|---|---|---|---|
| | | | | | Проект: Трёхкомнатная квартира | |
| | Лист | № док. | Подпись | Дата | | |
| Дизайнер | Кырлан А.С. | | | 05.10.26 | Визуализация ванной | Стадия / Лист / Листов |
| | | | | | | П / 44 / 89 |

выпуск 05.10.2026 № 6a37468da7 · стр. 44 из 89

## Развёртка стены А

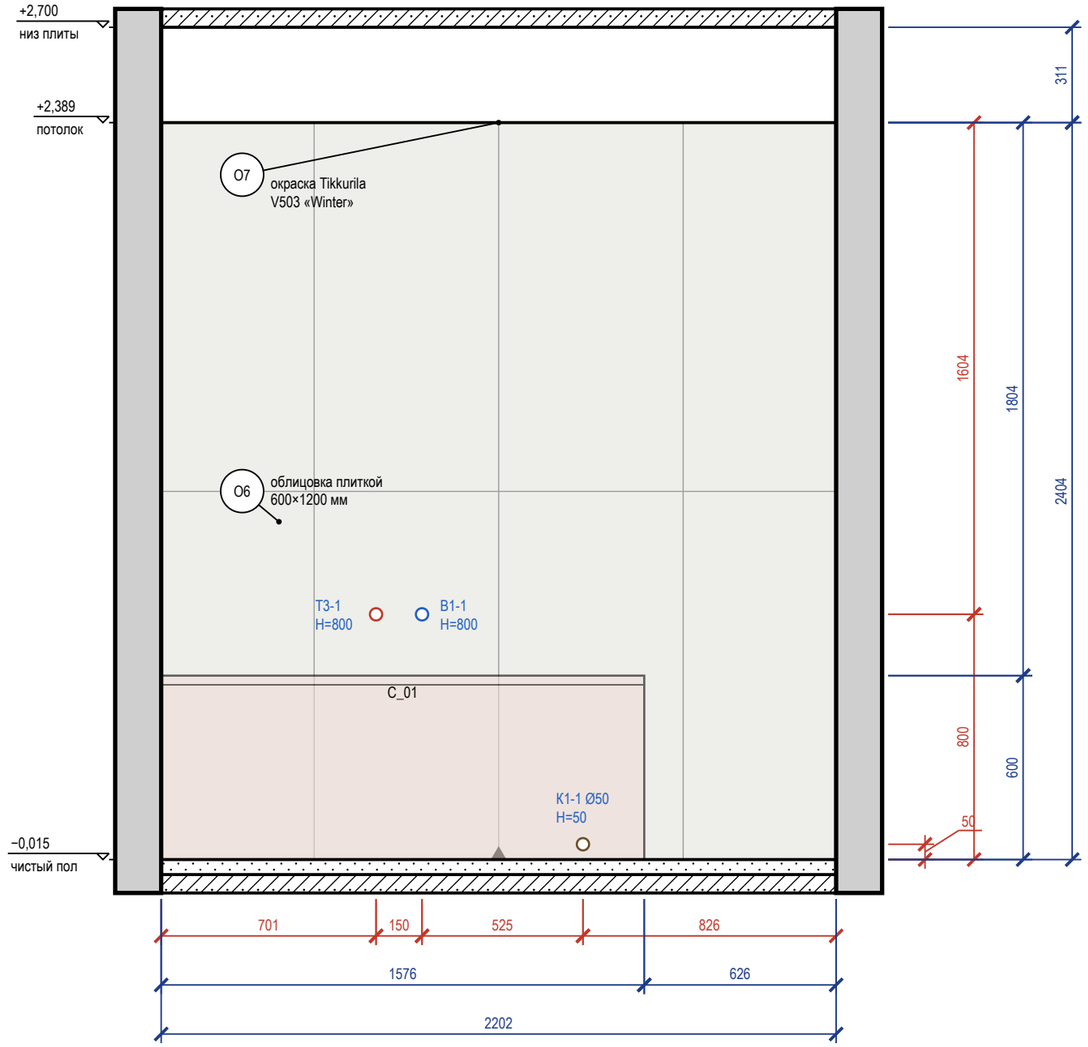


## Развёртка стены Б

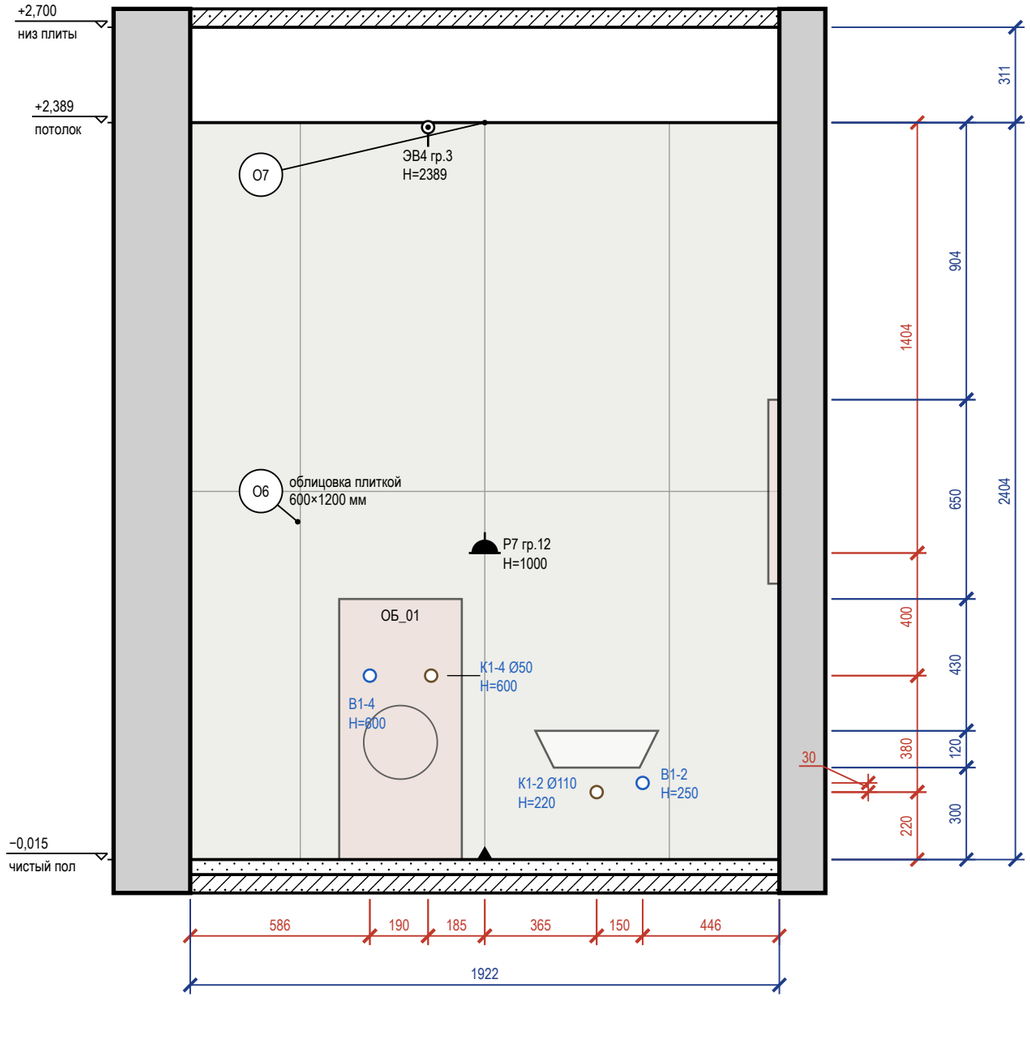


### Схема развёрток (М 1:100)

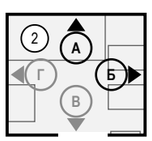


### Ведомость отделки (на листе)

| Марка | Поверхность | Материал, изделие | Цвет, код | Кол. |
|---|---|---|---|---|
| О6 | стены | облицовка плиткой, 600×1200×9 мм, аналог: керамогранит под травертин, матовый, затирка CG2WA | | 9,9 м² |
| О7 | потолок | окраска, Tikkurila Luja 7, матовая, подготовка Q3 | Tikkurila V503 «Winter» | 4,4 м² |

Визуализация этой стены — лист 41

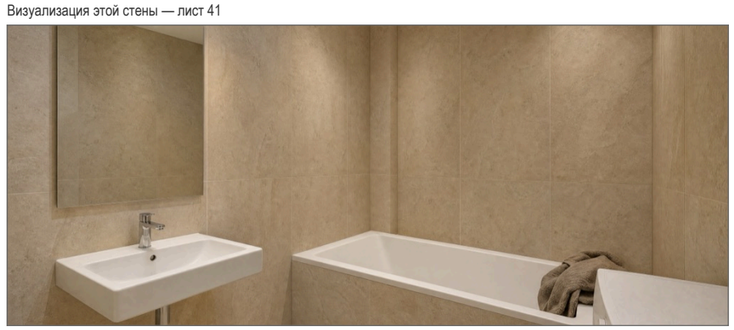

### Примечания

1. Размеры — в мм от чистовых поверхностей стен; условные обозначения и общие указания — лист 2.
2. Схема мебели, приборов и декора не является технической документацией для производства мебели; габариты — по паспортам изделий.
3. Выводы ВК — коды и высоты по листу выводов сантехники.
4. Облицовка — по сетке швов 2 мм, раскладка от оси стены (треугольник у пола), целые ряды от пола; подрезки — по листу раскладки плитки.
5. Гидроизоляция в 2 слоя, заход на стены 200 мм — до облицовки, с актом скрытых работ и тестом проливом (узел — на листе узлов).

| | | | | | |
|---|---|---|---|---|---|
| | | | | | Проект: Трёхкомнатная квартира |
| | Лист | № док. | Подпись | Дата | Развёртки стен А, Б. Ванная (пом. 2) |
| Дизайнер | Кырлан А.С. | | | 05.10.26 | |

| Стадия | Лист | Листов |
|---|---|---|
| П | 45 | 89 |

выпуск 05.10.2026 № 6a37468da7 · стр. 45 из 89

## Развёртка стены В

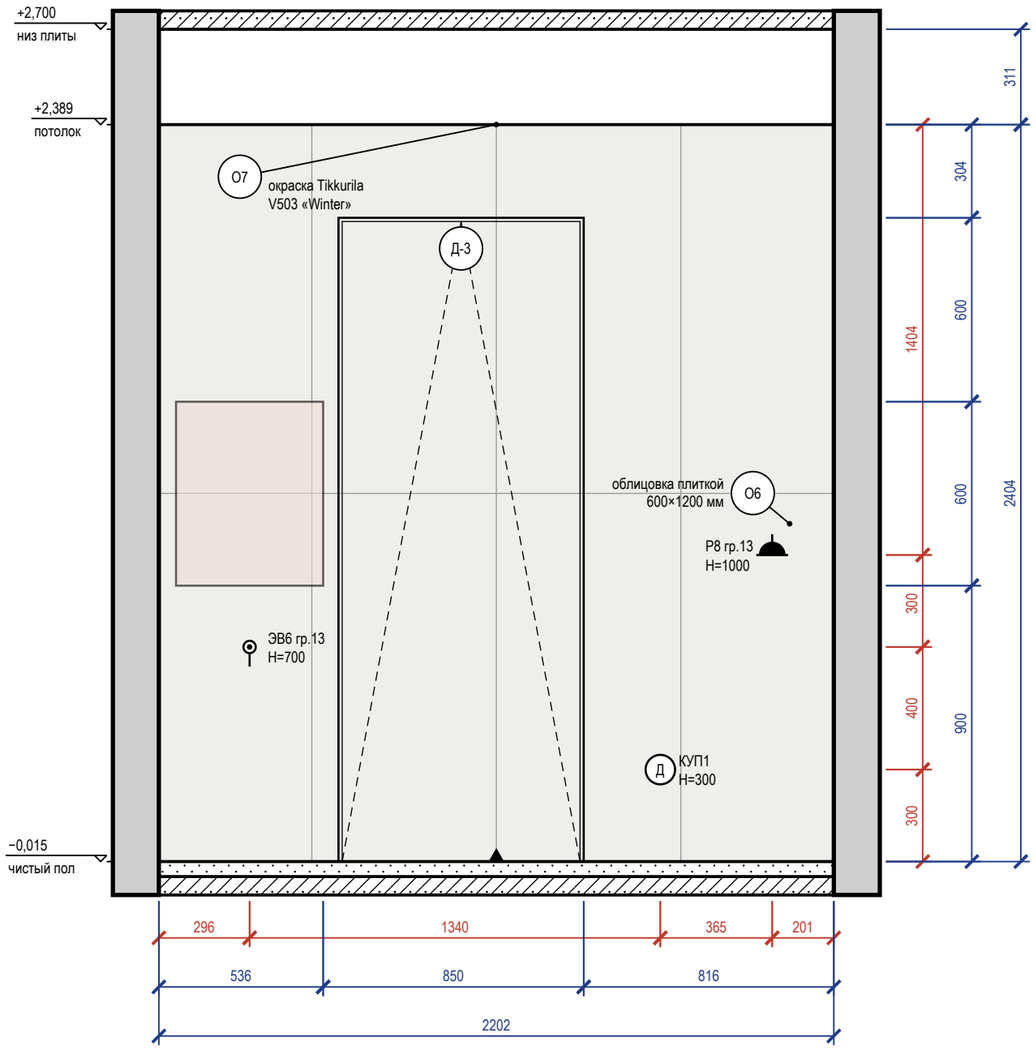


## Схема развёрток (М 1:100)

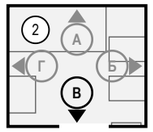


## Ведомость отделки (на листе)

| Марка | Поверхность | Материал, изделие | Цвет, код | Кол. |
|---|---|---|---|---|
| О6 | стены | облицовка плиткой, 600×1200×9 мм, аналог: керамогранит под травертин, матовый, затирка CG2WA | | 3,6 м² |
| О7 | потолок | окраска, Tikkurila Luja 7, матовая, подготовка Q3 | Tikkurila V503 «Winter» | 4,4 м² |

Визуализация этой стены — лист 43

## Примечания

1. Размеры — в мм от чистовых поверхностей стен; условные обозначения и общие указания — лист 2.
2. Схема мебели, приборов и декора не является технической документацией для производства мебели; габариты — по паспортам изделий.
3. Облицовка — по сетке швов 2 мм, раскладка от оси стены (треугольник у пола), целые ряды от пола; подрезки — по листу раскладки плитки.
4. Гидроизоляция в 2 слоя, заход на стены 200 мм — до облицовки, с актом скрытых работ и тестом проливом (узел — на листе узлов).
5. Двери скрытого монтажа — полотно в плоскости стены, отделка стены по полотну, плинтус прерывается у короба (узел — на листе узлов).

| | | | | | |
|---|---|---|---|---|---|
| | | | | | Проект: Трёхкомнатная квартира |
| | Лист | № док. | Подпись | Дата | |
| Дизайнер | Кырлан А.С. | | | 05.10.26 | Развёртка стены В. Ванная (пом. 2) |

| Стадия | Лист | Листов |
|---|---|---|
| П | 46 | 89 |

выпуск 05.10.2026 № 6a37468da7 · стр. 46 из 89

## Развёртка стены Г

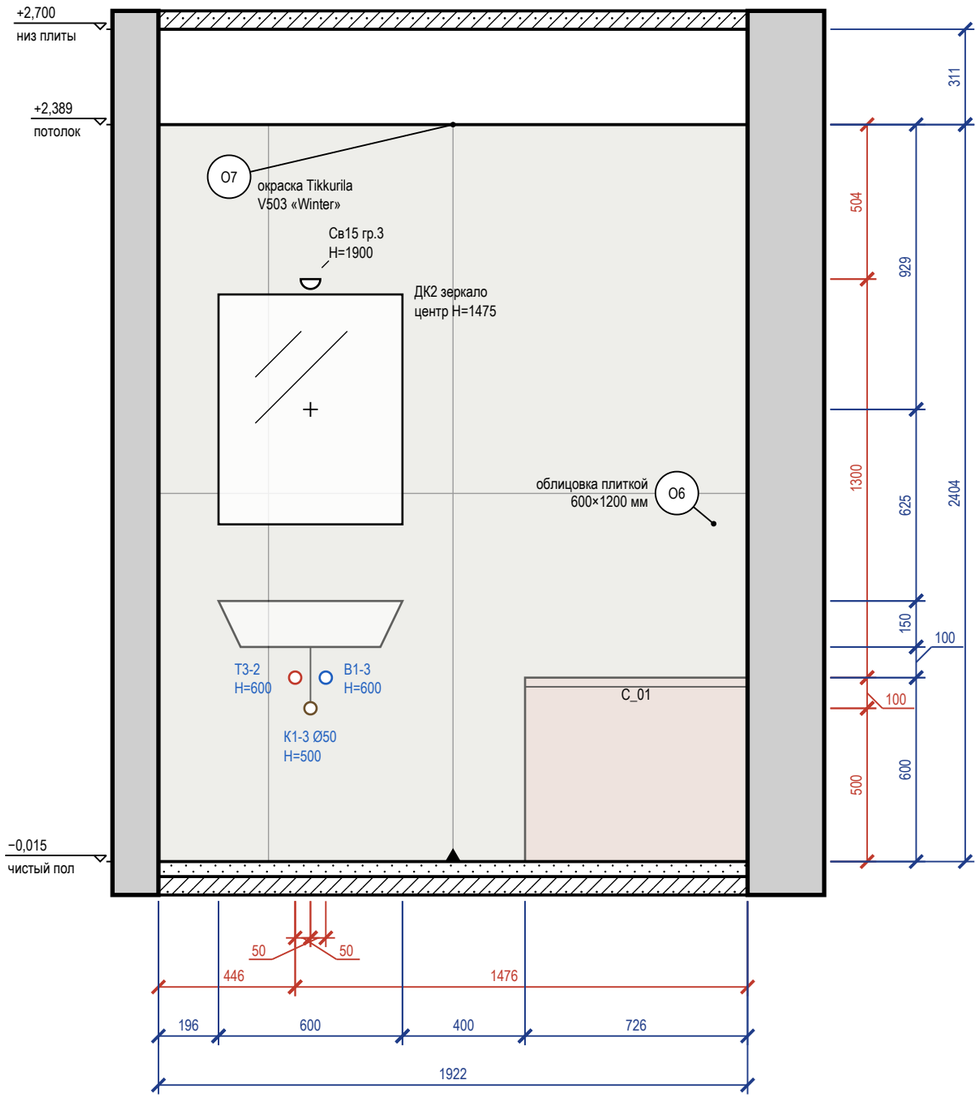


## Схема развёрток (М 1:100)

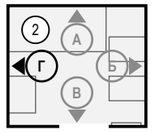


## Ведомость отделки (на листе)

| Марка | Поверхность | Материал, изделие | Цвет, код | Кол. |
|---|---|---|---|---|
| О6 | стены | облицовка плиткой, 600×1200×9 мм, аналог: керамогранит под травертин, матовый, затирка CG2WA | | 4,6 м² |
| О7 | потолок | окраска, Tikkurila Luja 7, матовая, подготовка Q3 | Tikkurila V503 «Winter» | 4,4 м² |

Визуализация этой стены — лист 44

## Примечания

1. Размеры — в мм от чистовых поверхностей стен; условные обозначения и общие указания — лист 2.
2. Схема мебели, приборов и декора не является технической документацией для производства мебели; габариты — по паспортам изделий.
3. Выводы ВК — коды и высоты по листу выводов сантехники.
4. Облицовка — по сетке швов 2 мм, раскладка от оси стены (треугольник у пола), целые ряды от пола; подрезки — по листу раскладки плитки.
5. Гидроизоляция в 2 слоя, заход на стены 200 мм — до облицовки, с актом скрытых работ и тестом проливом (узел — на листе узлов).
6. Картины и зеркала крепить к основанию по паспорту изделия (закладные и анкеры — в перечне скрытых работ); крест — ось центра предмета.

| | | | | | |
|---|---|---|---|---|---|
| | | | | | Проект: Трёхкомнатная квартира |
| | Лист | № док. | Подпись | Дата | |
| Дизайнер | Кырлан А.С. | | | 05.10.26 | Развёртка стены Г. Ванная (пом. 2) |

| Стадия | Лист | Листов |
|---|---|---|
| П | 47 | 89 |

выпуск 05.10.2026 № 6a37468da7 · стр. 47 из 89

| | | | | | |
|---|---|---|---|---|---|
| | | | | | Проект: Трёхкомнатная квартира |
| | | | | | |
| | Лист | № док. | Подпись | Дата | |
| Дизайнер | Кырлан А.С. | | | 05.10.26 | Визуализация гардеробной |
| | | | | | |

| Стадия | Лист | Листов |
|---|---|---|
| П | 48 | 89 |

выпуск 05.10.2026 № 6a37468da7 · стр. 48 из 89

## Развёртка стены А

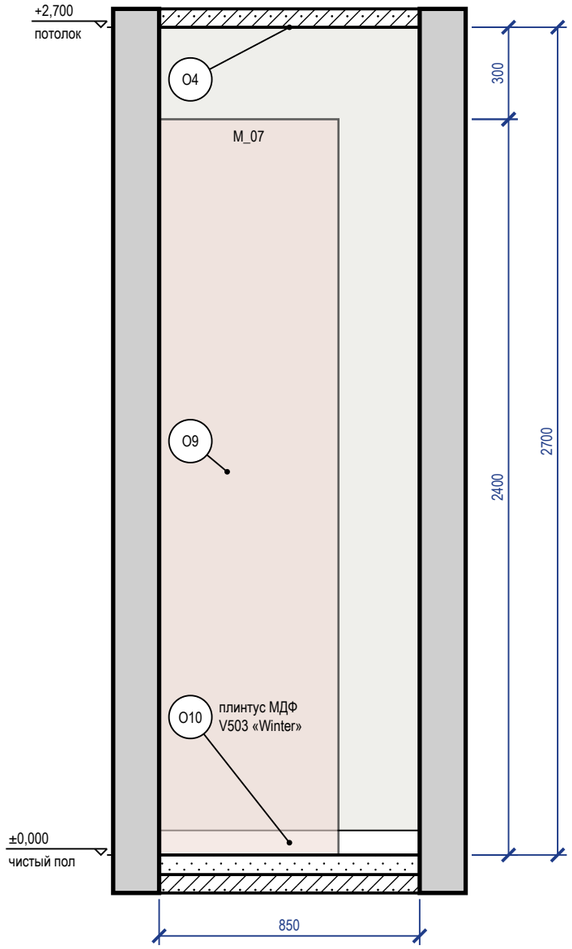


## Развёртка стены В

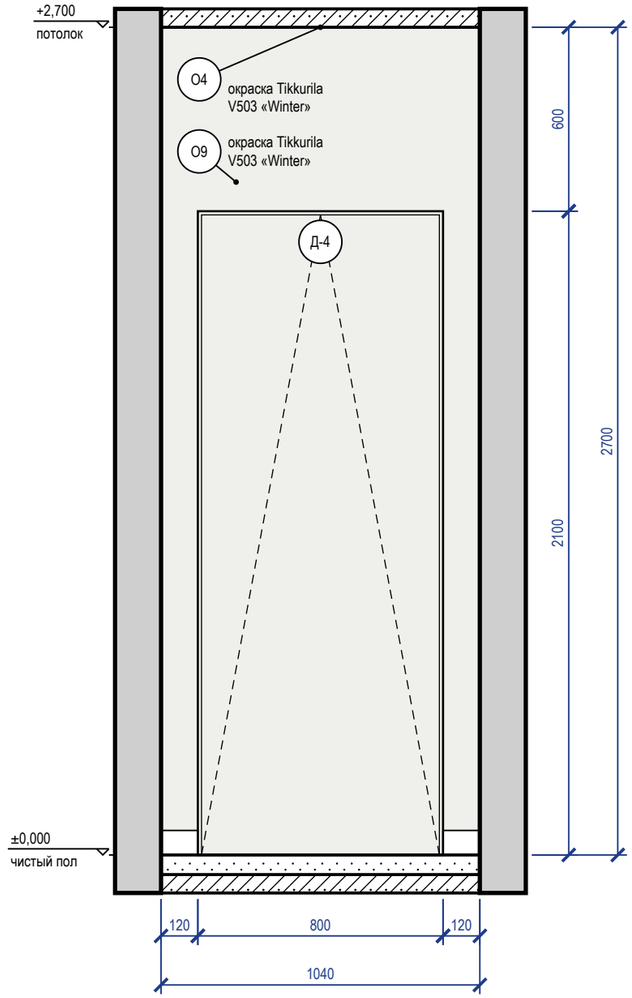


## Развёртка стены Г

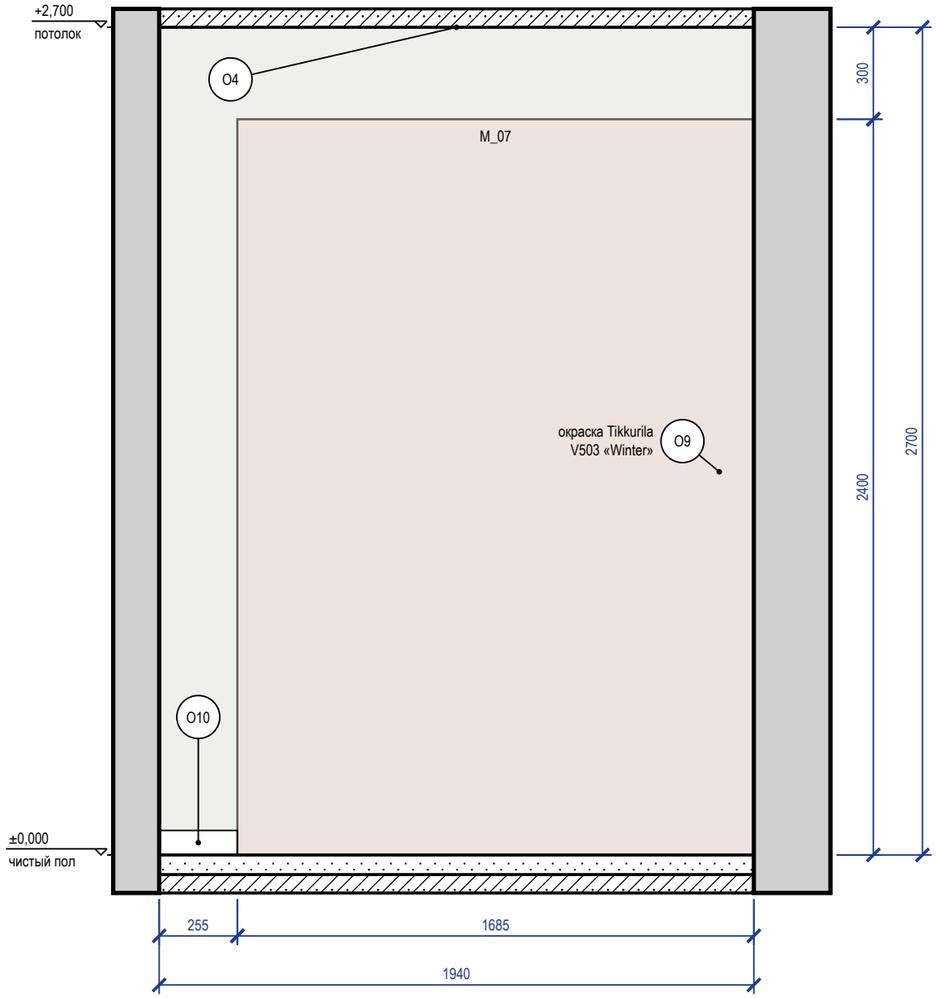


### Схема развёрток (М 1:100)

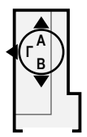


### Ведомость отделки (на листе)

| Марка | Поверхность | Материал, изделие | Цвет, код | Кол. |
|---|---|---|---|---|
| О4 | потолок | окраска, Tikkurila Anti-Reflex 2, глубокоматовая, подготовка Q3 | Tikkurila V503 «Winter» | 1,9 м² |
| О9 | стены | окраска, Tikkurila Harmony, матовая, подготовка Q3 | Tikkurila V503 «Winter» | 8,7 м² |
| О10 | плинтус | плинтус МДФ, h 80 мм, аналог: плинтус МДФ под покраску 80×16 | Tikkurila V503 «Winter» | 1,3 м |

Визуализация этой стены — лист 48

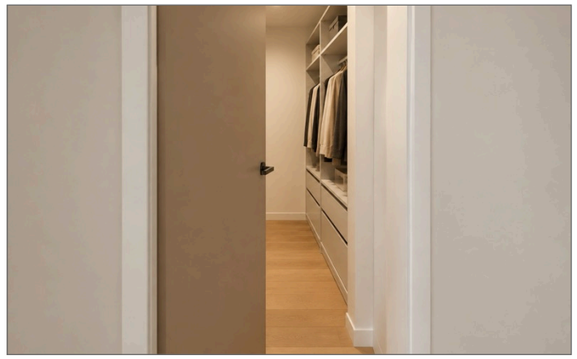

### Примечания

1. Размеры — в мм от чистовых поверхностей стен; условные обозначения и общие указания — лист 2.
2. Двери скрытого монтажа — полотно в плоскости стены, отделка стены по полотну, плинтус прерывается у короба (узел — на листе узлов).

| | | | | | |
|---|---|---|---|---|---|
| | | | | | Проект: Трёхкомнатная квартира |
| | Лист | № док. | Подпись | Дата | Развёртки стен. Гардеробная (пом. 3) |
| Дизайнер | Кырлан А.С. | | | 05.10.26 | |

| Стадия | Лист | Листов |
|---|---|---|
| П | 49 | 89 |

выпуск 05.10.2026 № 6a37468da7 · стр. 49 из 89

| | | | | | |
|---|---|---|---|---|---|
| | | | | | Проект: Трёхкомнатная квартира |
| | Лист | № док. | Подпись | Дата | |
| Дизайнер | Кырлан А.С. | | | 05.10.26 | Визуализация: Спальня 2 |
| | | | | | |

| Стадия | Лист | Листов |
|---|---|---|
| П | 50 | 89 |

выпуск 05.10.2026 № 6a37468da7 · стр. 50 из 89

| | | | | | |
|---|---|---|---|---|---|
| | | | | | Проект: Трёхкомнатная квартира |
| | | | | | |
| | Лист | № док. | Подпись | Дата | |
| Дизайнер | Кырлан А.С. | | | 05.10.26 | Визуализация: Спальня 2 |
| | | | | | |

| Стадия | Лист | Листов |
|---|---|---|
| П | 51 | 89 |

выпуск 05.10.2026 № 6a37468da7 · стр. 51 из 89

| | | | | | |
|---|---|---|---|---|---|
| | | | | | Проект: Трёхкомнатная квартира |
| | | | | | |
| | Лист | № док. | Подпись | Дата | |
| Дизайнер | Кырлан А.С. | | | 05.10.26 | Визуализация: Спальня 2 |
| | | | | | |

| Стадия | Лист | Листов |
|---|---|---|
| П | 52 | 89 |

выпуск 05.10.2026 № 6a37468da7 · стр. 52 из 89

## Развёртка стены А

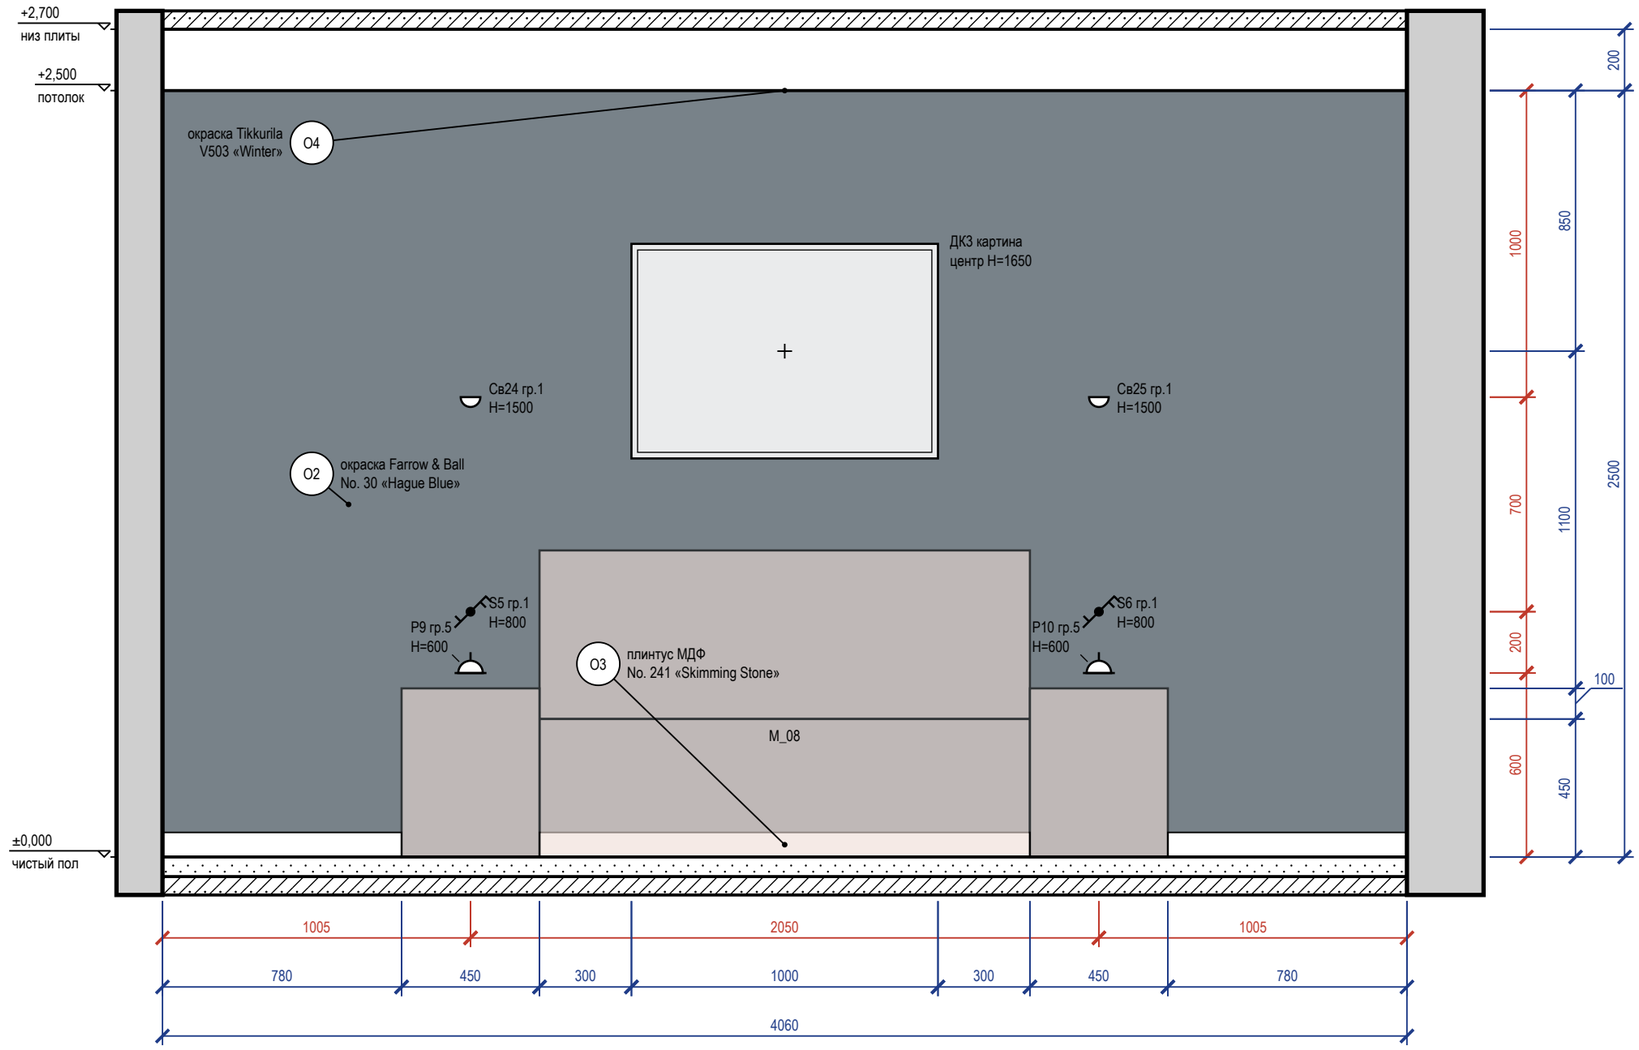


Визуализация этой стены — лист 51

### Схема развёрток (М 1:100)

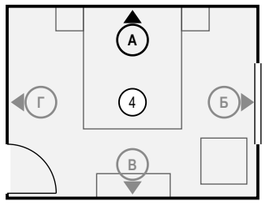


### Ведомость отделки (на листе)

| Марка | Поверхность | Материал, изделие | Цвет, код | Кол. |
|---|---|---|---|---|
| О2 | акцентная стена | окраска, Farrow & Ball Modern Emulsion, матовая, подготовка Q3 | Farrow & Ball No. 30 «Hague Blue» | 10,2 м² |
| О3 | плинтус | плинтус МДФ, h 80 мм, аналог: плинтус МДФ под покраску 80×16 | Farrow & Ball No. 241 «Skimming Stone» | 3,2 м |
| О4 | потолок | окраска, Tikkurila Anti-Reflex 2, глубокоматовая, подготовка Q3 | Tikkurila V503 «Winter» | 12,8 м² |

### Примечания

1. Размеры — в мм от чистовых поверхностей стен; условные обозначения и общие указания — лист 2.
2. Картины и зеркала крепить к основанию по паспорту изделия (закладные и анкеры — в перечне скрытых работ); крест — ось центра предмета.
3. Потолок на развёртках — по нижнему уровню У1; другие уровни потолка помещения: У2 +2,600.

| | | | | | |
|---|---|---|---|---|---|
| | | | | | Проект: Трёхкомнатная квартира |
| | Лист | № док. | Подпись | Дата | |
| Дизайнер | Кырлан А.С. | | | 05.10.26 | Развёртка стены А. Спальня 2 (пом. 4) |
| | | | | | Стадия: П; Лист: 53; Листов: 89 |

выпуск 05.10.2026 № 6a37468da7 · стр. 53 из 89

## Развёртка стены Б

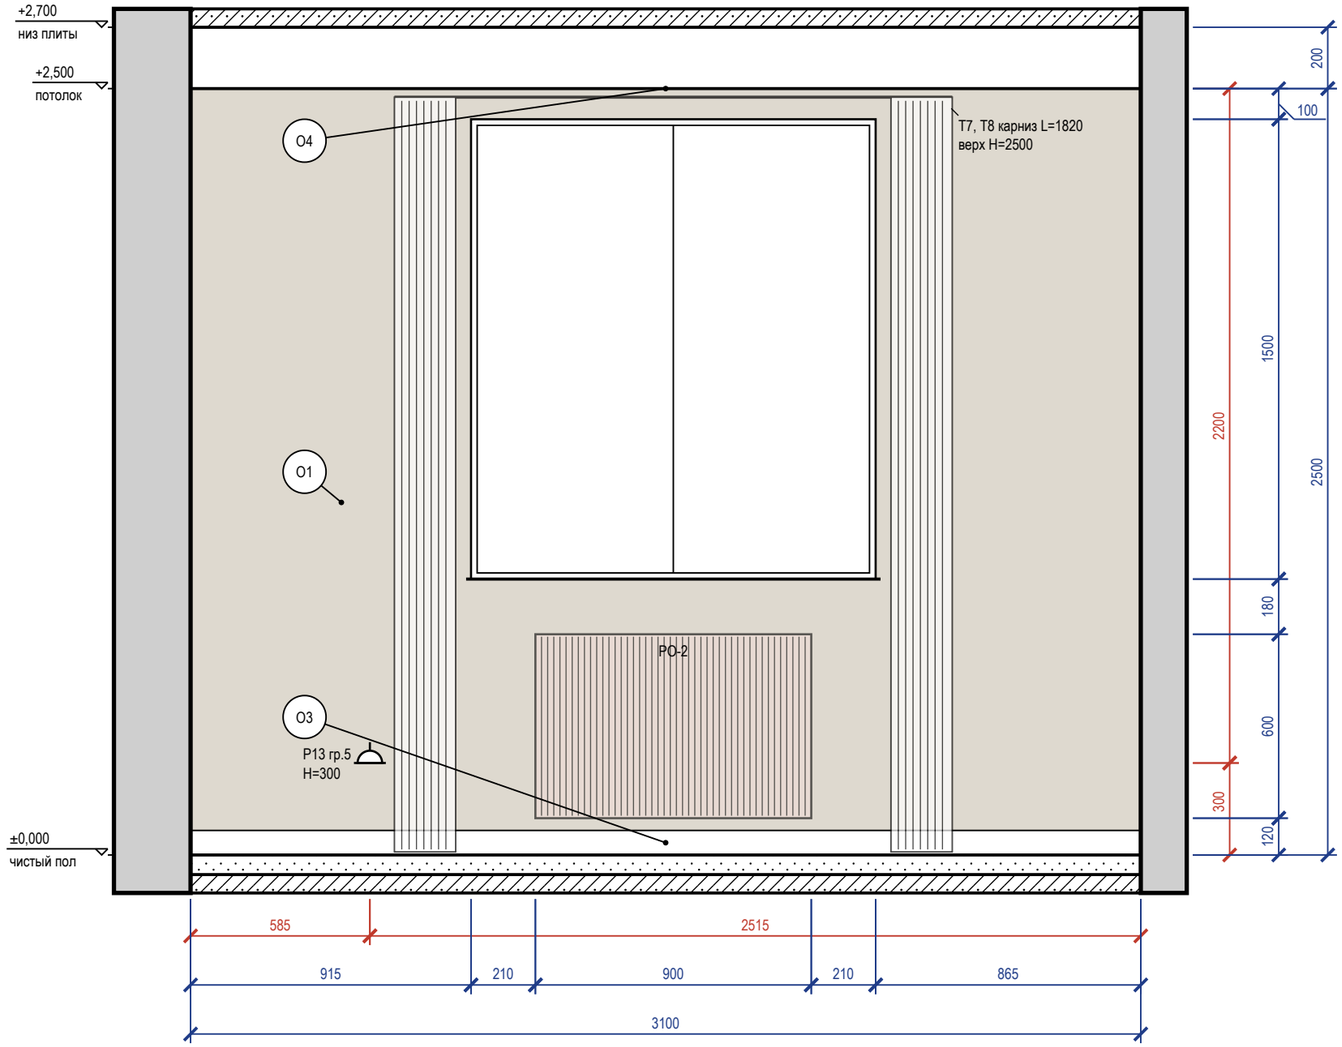


## Схема развёрток (М 1:100)

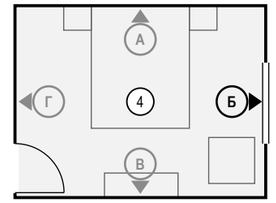


## Ведомость отделки (на листе)

| Марка | Поверхность | Материал, изделие | Цвет, код | Кол. |
|---|---|---|---|---|
| О1 | стены | окраска, Farrow & Ball Modern Emulsion, матовая, подготовка Q3 | Farrow & Ball No. 241 «Skimming Stone» | 5,8 м² |
| О3 | плинтус | плинтус МДФ, h 80 мм, аналог: плинтус МДФ под покраску 80×16 | Farrow & Ball No. 241 «Skimming Stone» | 3,1 м |
| О4 | потолок | окраска, Tikkurila Anti-Reflex 2, глубокоматовая, подготовка Q3 | Tikkurila V503 «Winter» | 12,8 м² |

Визуализация этой стены — лист 50

## Примечания

1. Размеры — в мм от чистовых поверхностей стен; условные обозначения и общие указания — лист 2.
2. Карнизы (шины) — по ведомости текстиля декоратора; длина L и верх H — по развёртке, крепление — до окраски потолка.
3. Потолок на развёртках — по нижнему уровню У1; другие уровни потолка помещения: У2 +2,600.

| | | | | | |
|---|---|---|---|---|---|
| | | | | | Проект: Трёхкомнатная квартира |
| | Лист | № док. | Подпись | Дата | Развёртка стены Б. Спальня 2 (пом. 4) |
| Дизайнер | Кырлан А.С. | | | 05.10.26 | |

| Стадия | Лист | Листов |
|---|---|---|
| П | 54 | 89 |

выпуск 05.10.2026 № 6a37468da7 · стр. 54 из 89

## Развёртка стены В

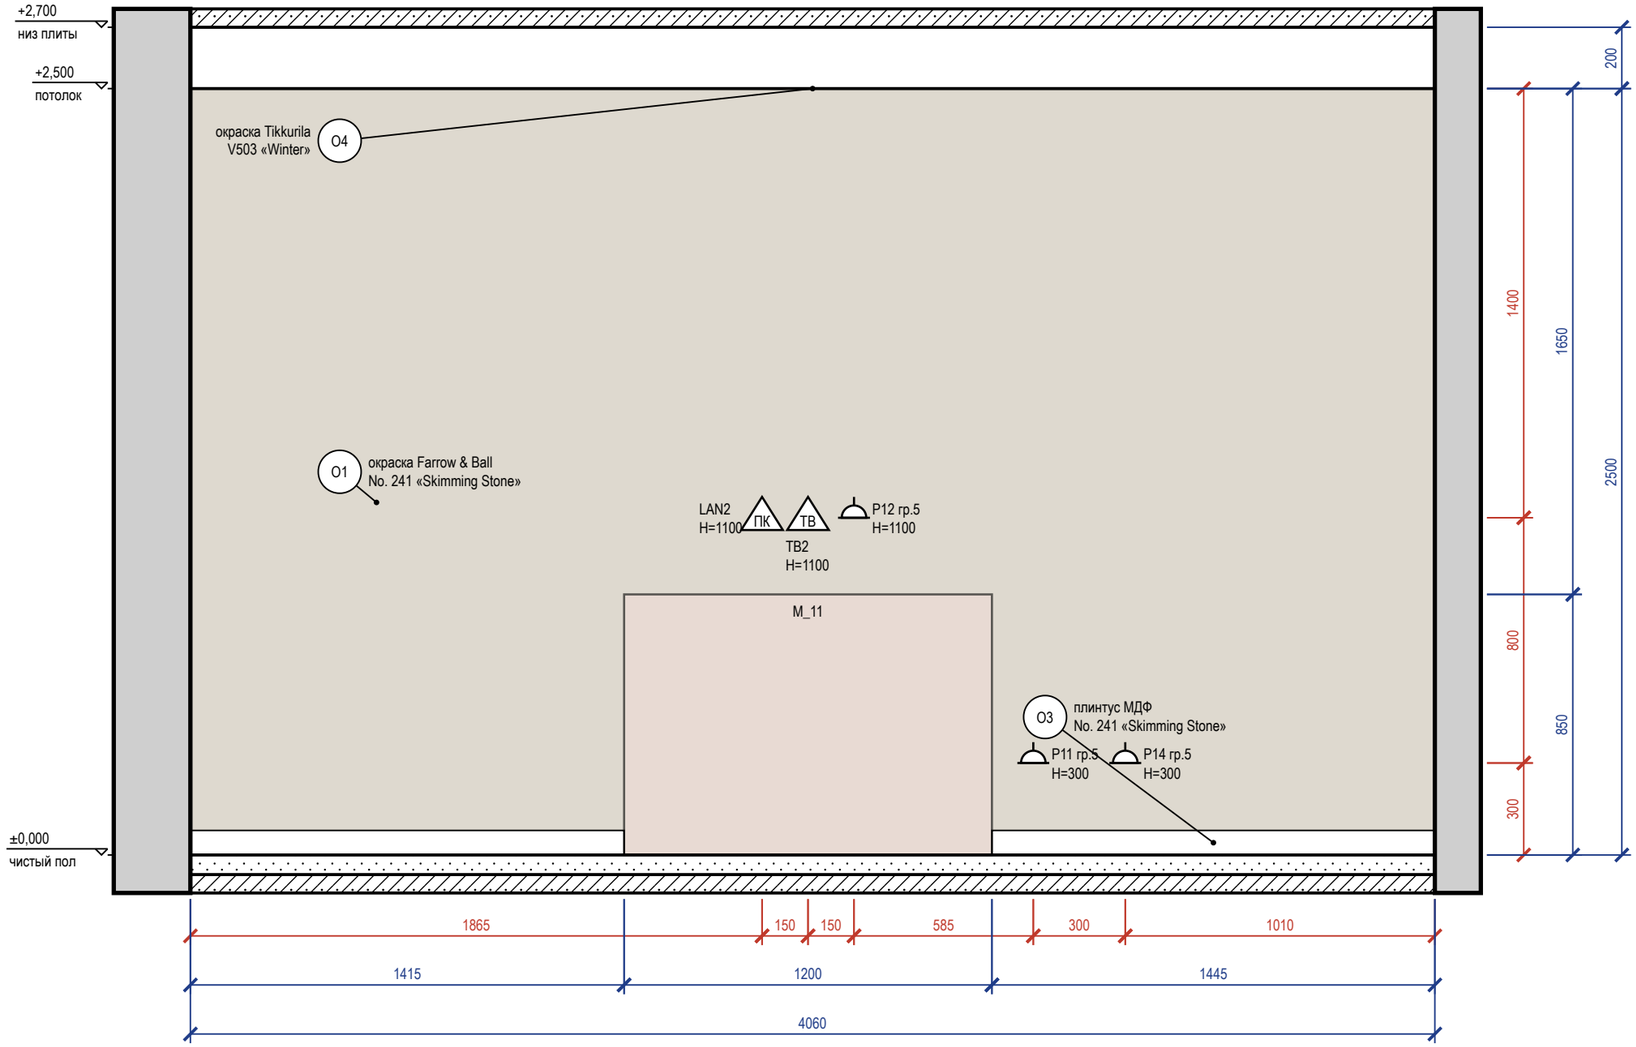


### Схема развёрток (М 1:100)

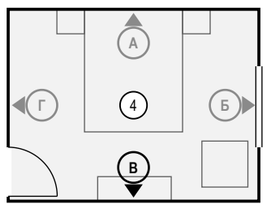


### Ведомость отделки (на листе)

| Марка | Поверхность | Материал, изделие | Цвет, код | Кол. |
|---|---|---|---|---|
| O1 | стены | окраска, Farrow & Ball Modern Emulsion, матовая, подготовка Q3 | Farrow & Ball No. 241 «Skimming Stone» | 10,2 м² |
| O3 | плинтус | плинтус МДФ, h 80 мм, аналог: плинтус МДФ под покраску 80×16 | Farrow & Ball No. 241 «Skimming Stone» | 2,9 м |
| O4 | потолок | окраска, Tikkurila Anti-Reflex 2, глубокоматовая, подготовка Q3 | Tikkurila V503 «Winter» | 12,8 м² |

### Примечания

1. Размеры — в мм от чистовых поверхностей стен; условные обозначения и общие указания — лист 2.
2. Потолок на развёртках — по нижнему уровню У1; другие уровни потолка помещения: У2 +2,600.

| | | | | | |
|---|---|---|---|---|---|
| | | | | | Проект: Трёхкомнатная квартира |
| | Лист | № док. | Подпись | Дата | Развёртка стены В. Спальня 2 (пом. 4) |
| Дизайнер | Кырлан А.С. | | | 05.10.26 | |

| Стадия | Лист | Листов |
|---|---|---|
| П | 55 | 89 |

выпуск 05.10.2026 № 6a37468da7 · стр. 55 из 89

## Развёртка стены Г

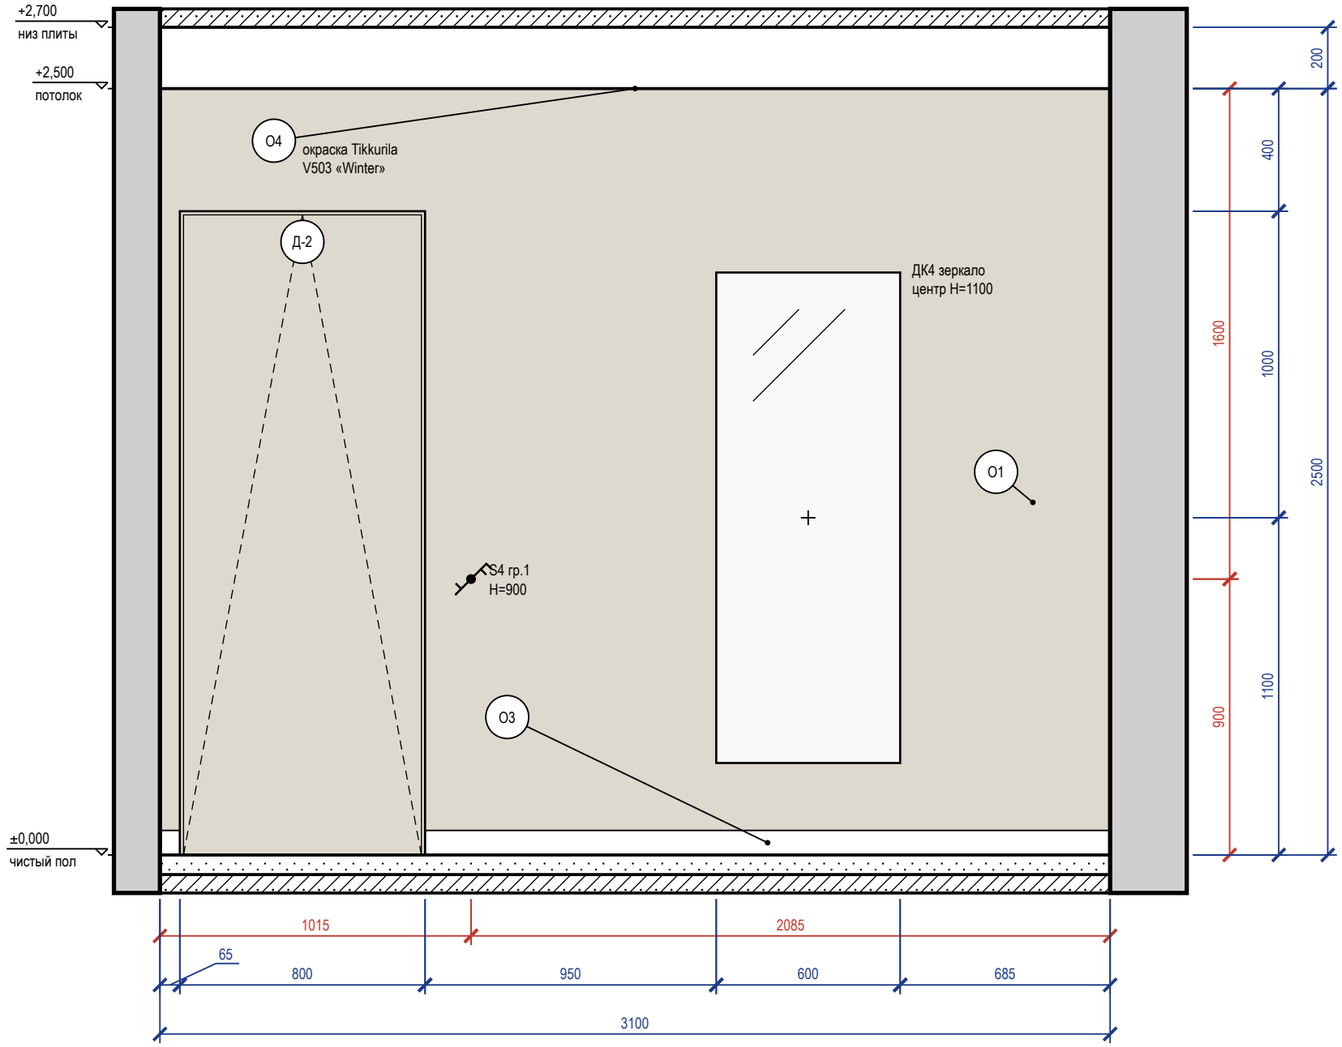


## Схема развёрток (М 1:100)

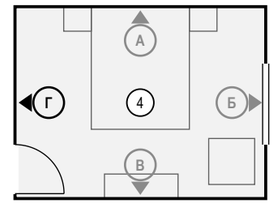


## Ведомость отделки (на листе)

| Марка | Поверхность | Материал, изделие | Цвет, код | Кол. |
|---|---|---|---|---|
| О1 | стены | окраска, Farrow & Ball Modern Emulsion, матовая, подготовка Q3 | Farrow & Ball No. 241 «Skimming Stone» | 6,1 м² |
| О3 | плинтус | плинтус МДФ, h 80 мм, аналог: плинтус МДФ под покраску 80×16 | Farrow & Ball No. 241 «Skimming Stone» | 2,3 м |
| О4 | потолок | окраска, Tikkurila Anti-Reflex 2, глубокоматовая, подготовка Q3 | Tikkurila V503 «Winter» | 12,8 м² |

Визуализация этой стены — лист 52

## Примечания

1. Размеры — в мм от чистовых поверхностей стен; условные обозначения и общие указания — лист 2.
2. Картины и зеркала крепить к основанию по паспорту изделия (закладные и анкеры — в перечне скрытых работ); крест — ось центра предмета.
3. Двери скрытого монтажа — полотно в плоскости стены, отделка стены по полотну, плинтус прерывается у короба (узел — на листе узлов).
4. Потолок на развёртках — по нижнему уровню У1; другие уровни потолка помещения: У2 +2,600.

| | | | | | |
|---|---|---|---|---|---|
| | | | | | Проект: Трёхкомнатная квартира |
| | Лист | № док. | Подпись | Дата | |
| Дизайнер | Кырлан А.С. | | | 05.10.26 | Развёртка стены Г. Спальня 2 (пом. 4) |

| Стадия | Лист | Листов |
|---|---|---|
| П | 56 | 89 |

выпуск 05.10.2026 № 6a37468da7 · стр. 56 из 89

| | | | | | |
|---|---|---|---|---|---|
| | | | | | Проект: Трёхкомнатная квартира |
| | Лист | № док. | Подпись | Дата | |
| Дизайнер | Кырлан А.С. | | | 05.10.26 | Визуализация прихожей |

| Стадия | Лист | Листов |
|---|---|---|
| П | 57 | 89 |

выпуск 05.10.2026 № 6a37468da7 · стр. 57 из 89

| | | | | | | |
|---|---|---|---|---|---|---|
| | | | | | Проект: Трёхкомнатная квартира | |
| | Лист | № док. | Подпись | Дата | | |
| Дизайнер | Кырлан А.С. | | | 05.10.26 | Визуализация прихожей | Стадия / Лист / Листов |
| | | | | | | П / 58 / 89 |

выпуск 05.10.2026 · 6a37468da7 · стр. 58 из 89

## Развёртка стены А

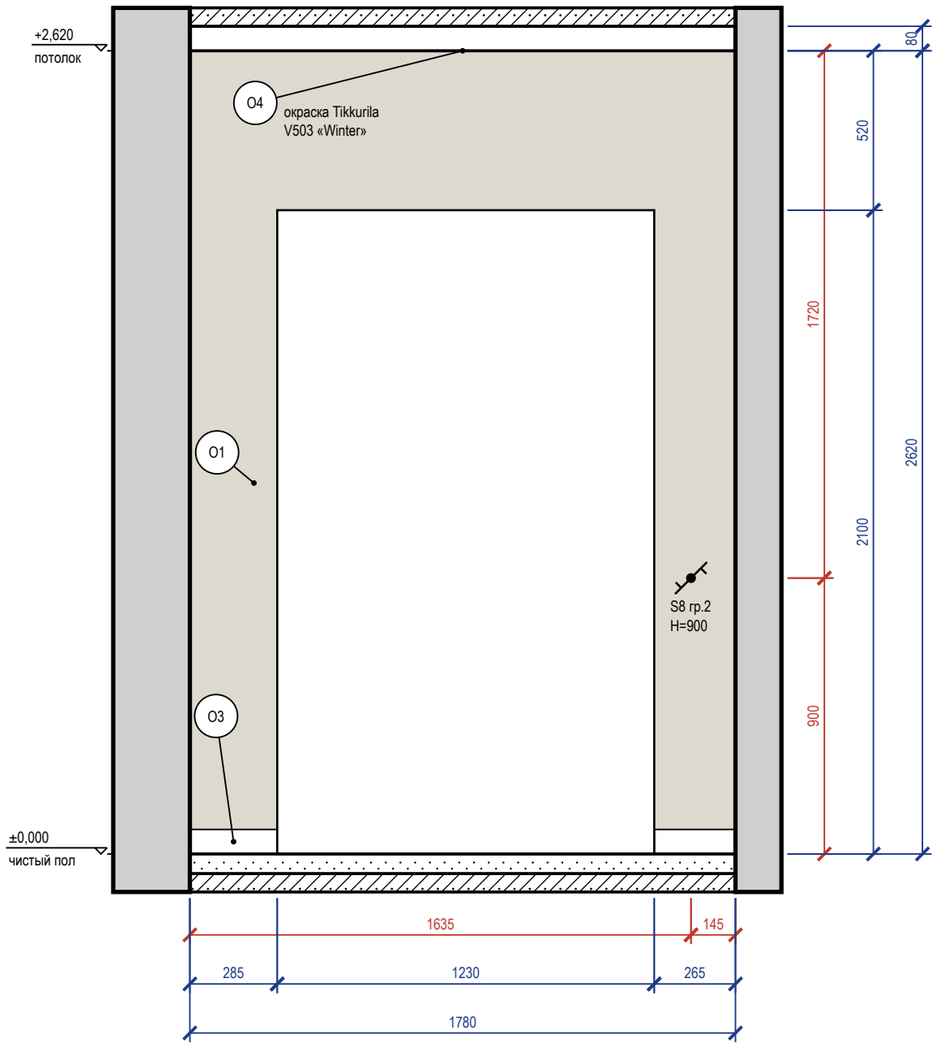


## Схема развёрток (М 1:100)

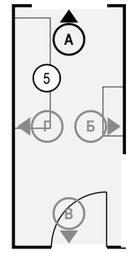


## Ведомость отделки (на листе)

| Марка | Поверхность | Материал, изделие | Цвет, код | Кол. |
|---|---|---|---|---|
| О1 | стены | окраска, Farrow & Ball Modern Emulsion, матовая, подготовка Q3 | Farrow & Ball No. 241 «Skimming Stone» | 2,1 м² |
| О3 | плинтус | плинтус МДФ, h 80 мм, аналог: плинтус МДФ под покраску 80×16 | Farrow & Ball No. 241 «Skimming Stone» | 0,6 м |
| О4 | потолок | окраска, Tikkurila Anti-Reflex 2, глубокоматовая, подготовка Q3 | Tikkurila V503 «Winter» | 7,1 м² |

Визуализация этой стены — лист 57

### Примечания

1. Размеры — в мм от чистовых поверхностей стен; условные обозначения и общие указания — лист 2.

| | | | | | |
|---|---|---|---|---|---|
| | | | | | Проект: Трёхкомнатная квартира |
| | Лист | № док. | Подпись | Дата | |
| Дизайнер | Кырлан А.С. | | | 05.10.26 | Развёртка стены А. Прихожая (пом. 5) |

| Стадия | Лист | Листов |
|---|---|---|
| П | 59 | 89 |

выпуск 05.10.2026 № 6a37468da7 · стр. 59 из 89

## Развёртка стены Б

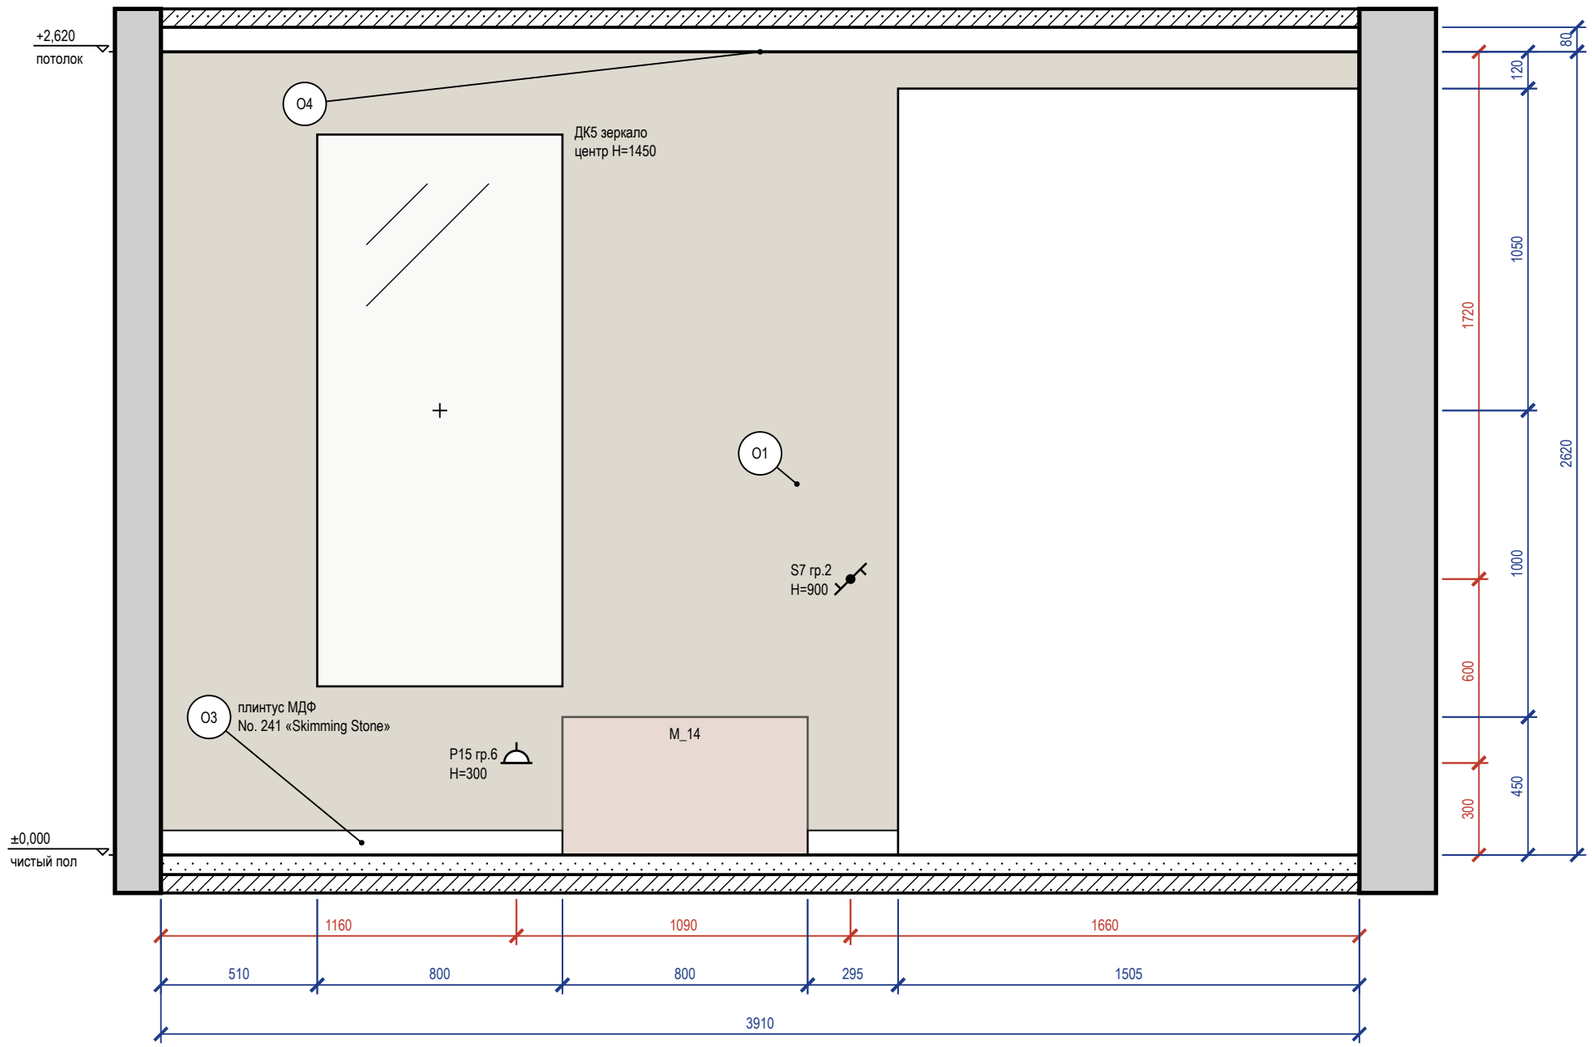


## Схема развёрток (М 1:100)

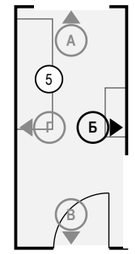


## Ведомость отделки (на листе)

| Марка | Поверхность | Материал, изделие | Цвет, код | Кол. |
|---|---|---|---|---|
| О1 | стены | окраска, Farrow & Ball Modern Emulsion, матовая, подготовка Q3 | Farrow & Ball No. 241 «Skimming Stone» | 6,5 м² |
| О3 | плинтус | плинтус МДФ, h 80 мм, аналог: плинтус МДФ под покраску 80×16 | Farrow & Ball No. 241 «Skimming Stone» | 1,6 м |
| О4 | потолок | окраска, Tikkurila Anti-Reflex 2, глубокоматовая, подготовка Q3 | Tikkurila V503 «Winter» | 7,1 м² |

**2** **Стык покрытий пола Т-профилем без перепада (М 1:5)**

Узел 2 — лист С3

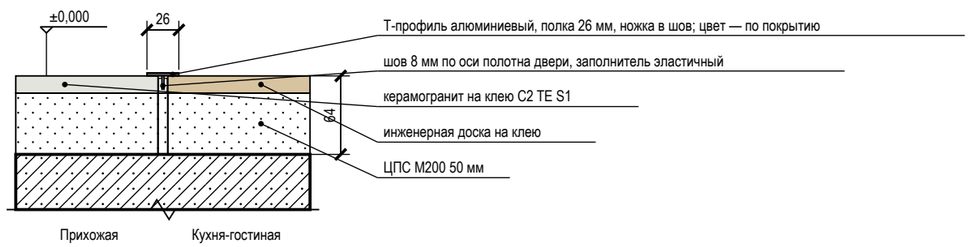


### Примечания

1. Размеры — в мм от чистовых поверхностей стен; условные обозначения и общие указания — лист 2.
2. Картины и зеркала крепить к основанию по паспорту изделия (закладные и анкеры — в перечне скрытых работ); крест — ось центра предмета.

| | | | | | |
|---|---|---|---|---|---|
| | | | | | Проект: Трёхкомнатная квартира |
| | Лист | № док. | Подпись | Дата | |
| Дизайнер | Кырлан А.С. | | | 05.10.26 | Развёртка стены Б. Прихожая (пом. 5) |

| Стадия | Лист | Листов |
|---|---|---|
| П | 60 | 89 |

выпуск 05.10.2026 № 6a37468da7 · стр. 60 из 89

## Развёртка стены В

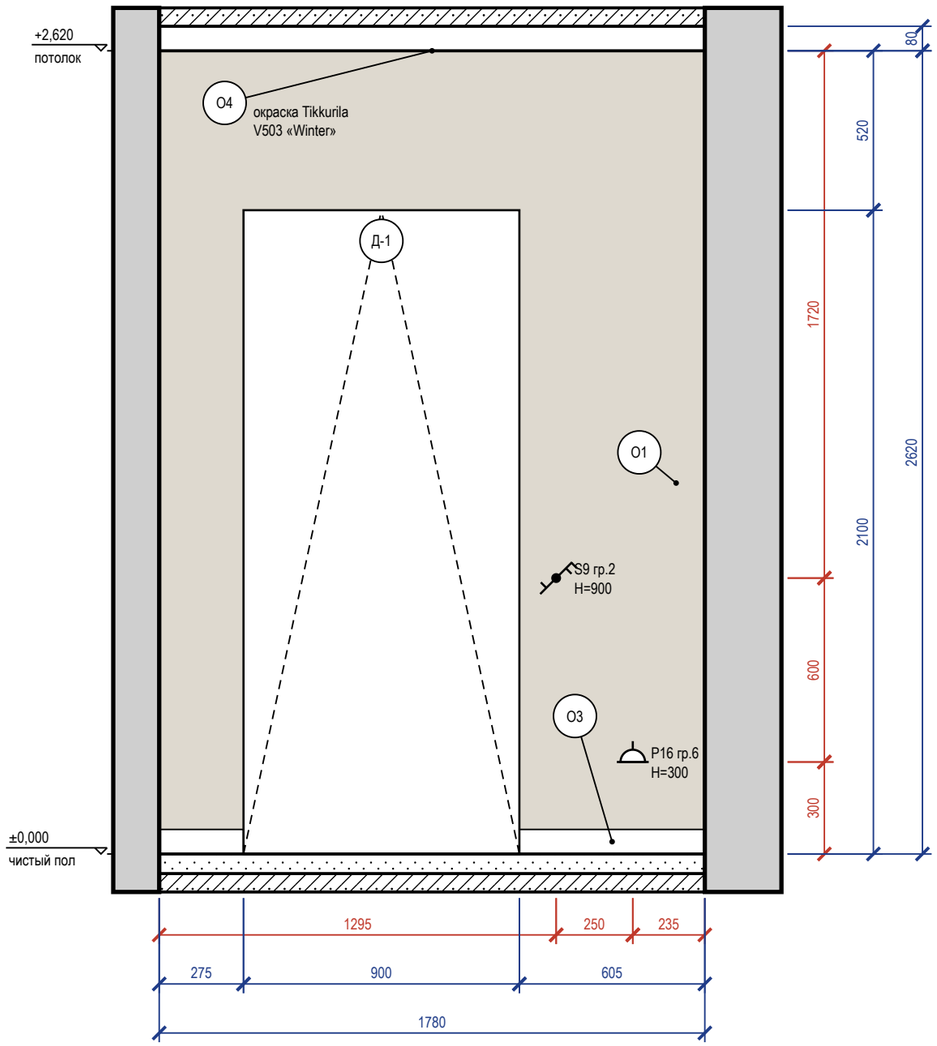


## Схема развёрток (М 1:100)

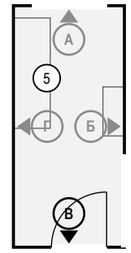


## Ведомость отделки (на листе)

| Марка | Поверхность | Материал, изделие | Цвет, код | Кол. |
|---|---|---|---|---|
| О1 | стены | окраска, Farrow & Ball Modern Emulsion, матовая, подготовка Q3 | Farrow & Ball No. 241 «Skimming Stone» | 2,8 м² |
| О3 | плинтус | плинтус МДФ, h 80 мм, аналог: плинтус МДФ под покраску 80×16 | Farrow & Ball No. 241 «Skimming Stone» | 0,9 м |
| О4 | потолок | окраска, Tikkurila Anti-Reflex 2, глубокоматовая, подготовка Q3 | Tikkurila V503 «Winter» | 7,1 м² |

Визуализация этой стены — лист 58

### Примечания

1. Размеры — в мм от чистовых поверхностей стен; условные обозначения и общие указания — лист 2.

| | | | | | |
|---|---|---|---|---|---|
| | | | | | Проект: Трёхкомнатная квартира |
| | Лист | № док. | Подпись | Дата | Развёртка стены В. Прихожая (пом. 5) |
| Дизайнер | Кырлан А.С. | | | 05.10.26 | |

| Стадия | Лист | Листов |
|---|---|---|
| П | 61 | 89 |

выпуск 05.10.2026 · 6a37468da7 · стр. 61 из 89

## Развёртка стены Г

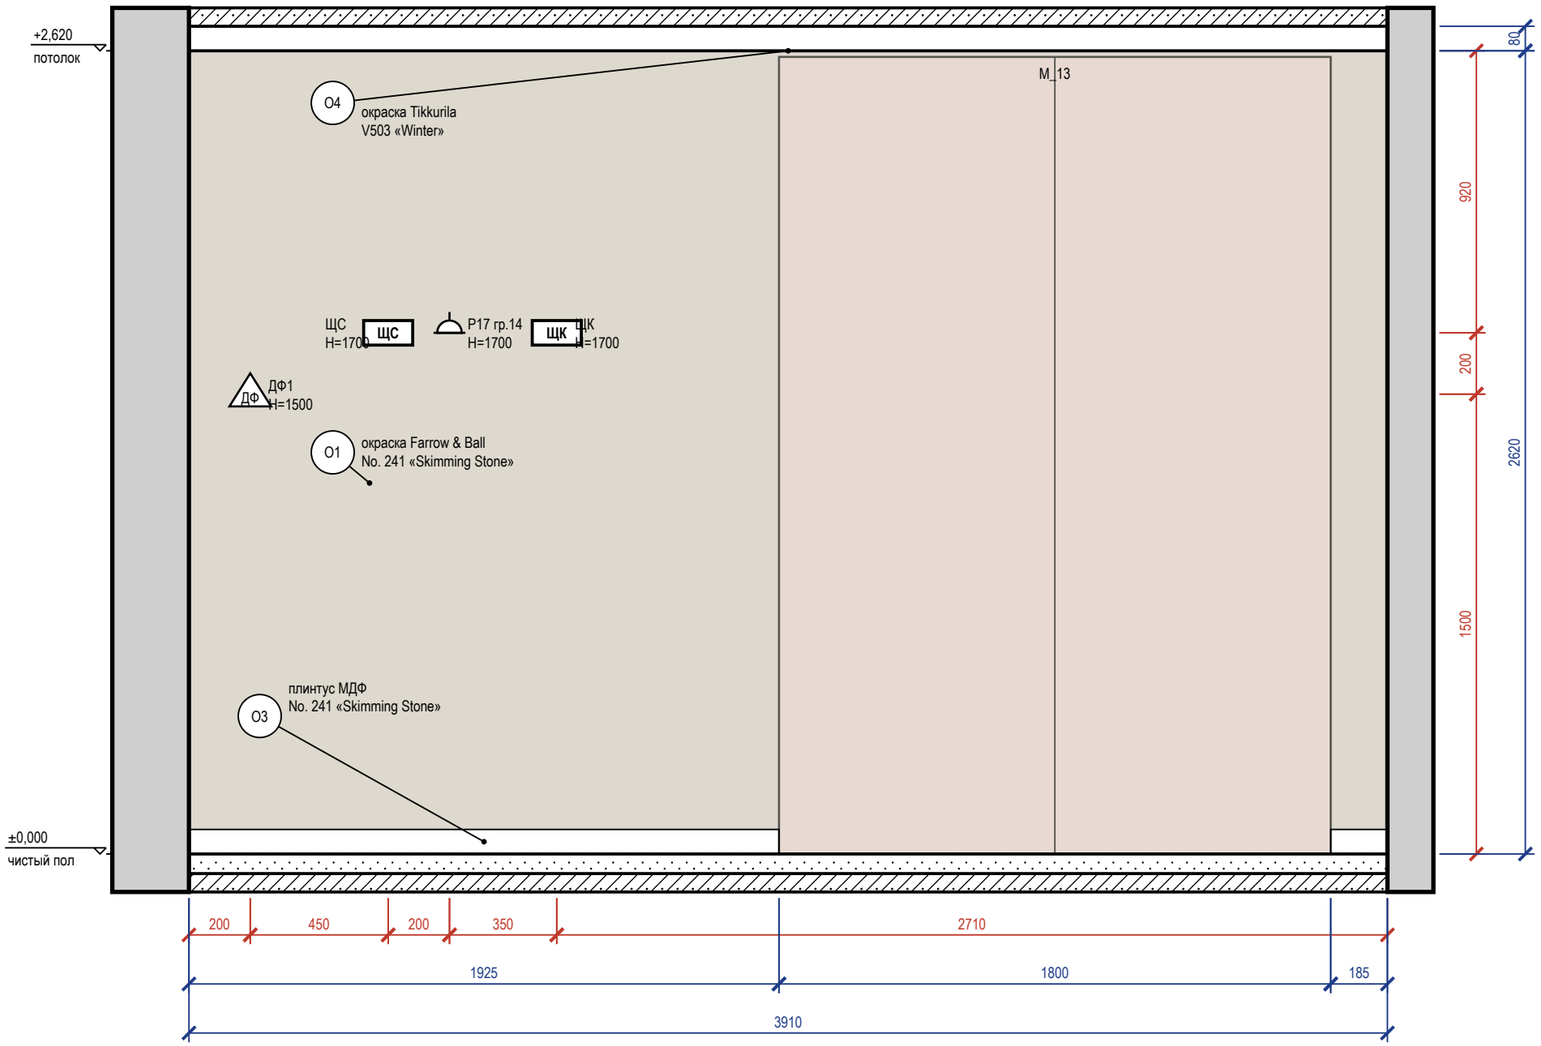


## Схема развёрток (М 1:100)

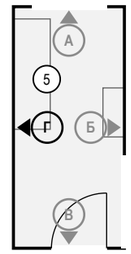


## Ведомость отделки (на листе)

| Марка | Поверхность | Материал, изделие | Цвет, код | Кол. |
|---|---|---|---|---|
| О1 | стены | окраска, Farrow & Ball Modern Emulsion, матовая, подготовка Q3 | Farrow & Ball No. 241 «Skimming Stone» | 10,2 м² |
| О3 | плинтус | плинтус МДФ, h 80 мм, аналог: плинтус МДФ под покраску 80×16 | Farrow & Ball No. 241 «Skimming Stone» | 2,1 м |
| О4 | потолок | окраска, Tikkurila Anti-Reflex 2, глубокоматовая, подготовка Q3 | Tikkurila V503 «Winter» | 7,1 м² |

## Примечания

1. Размеры — в мм от чистовых поверхностей стен; условные обозначения и общие указания — лист 2.

| | | | | | |
|---|---|---|---|---|---|
| | | | | | Проект: Трёхкомнатная квартира |
| | Лист | № док. | Подпись | Дата | Развёртка стены Г. Прихожая (пом. 5) |
| Дизайнер | Кырлан А.С. | | | 05.10.26 | |

| Стадия | Лист | Листов |
|---|---|---|
| П | 62 | 89 |

выпуск 05.10.2026 № 6a37468da7 · стр. 62 из 89

| | | | | | |
|---|---|---|---|---|---|
| | | | | | Проект: Трёхкомнатная квартира |
| | Лист | № док. | Подпись | Дата | |
| Дизайнер | Кырлан А. | С. | | 05.10.26 | Визуализация кухни-гостиной |

| Стадия | Лист | Листов |
|---|---|---|
| П | 63 | 89 |

выпуск 05.10.2026 № 6a37468da7 · стр. 63 из 89

| | | | | | | |
|---|---|---|---|---|---|---|
| | | | | | Проект: Трёхкомнатная квартира | |
| | Лист | № док. | Подпись | Дата | | |
| Дизайнер | Кырлан А.С. | | | 05.10.26 | Визуализация кухни-гостиной | Стадия / Лист / Листов |
| | | | | | | П / 64 / 89 |

выпуск 05.10.2026 № 6a37468da7 · стр. 64 из 89

| | | | | | | |
|---|---|---|---|---|---|---|
| | | | | | Проект: Трёхкомнатная квартира | |
| | | | | | | |
| | Лист | № док. | Подпись | Дата | | |
| Дизайнер | Кырлан А.С. | | | 05.10.26 | Визуализация кухни-гостиной | Стадия / Лист / Листов |
| | | | | | | П / 65 / 89 |

выпуск 05.10.2026 № 6a37468da7 · стр. 65 из 89

| | | | | | | |
|---|---|---|---|---|---|---|
| | | | | | Проект: Трёхкомнатная квартира | |
| | | | | | | |
| | Лист | № док. | Подпись | Дата | | |
| Дизайнер | Кырлан А.С. | | | 05.10.26 | Визуализация кухни-гостиной | Стадия / Лист / Листов |
| | | | | | | П / 66 / 89 |

выпуск 05.10.2026 № 6a37468da7 · стр. 66 из 89

| | | | | | |
|---|---|---|---|---|---|
| | | | | | Проект: Трёхкомнатная квартира |
| | Лист | № док. | Подпись | Дата | |
| Дизайнер | Кырлан А.С. | | | 05.10.26 | Визуализация кухни-гостиной |

| Стадия | Лист | Листов |
|---|---|---|
| П | 67 | 89 |

выпуск 05.10.2026 № 6a37468da7 · стр. 67 из 89

| | | | | | |
|---|---|---|---|---|---|
| | | | | | Проект: Трёхкомнатная квартира |
| | Лист | № док. | Подпись | Дата | |
| Дизайнер | Кырлан А.С. | | | 05.10.26 | Визуализация кухни-гостиной |

| Стадия | Лист | Листов |
|---|---|---|
| П | 68 | 89 |

выпуск 05.10.2026 № 6a37468da7 · стр. 68 из 89

## Развёртка стены Б2

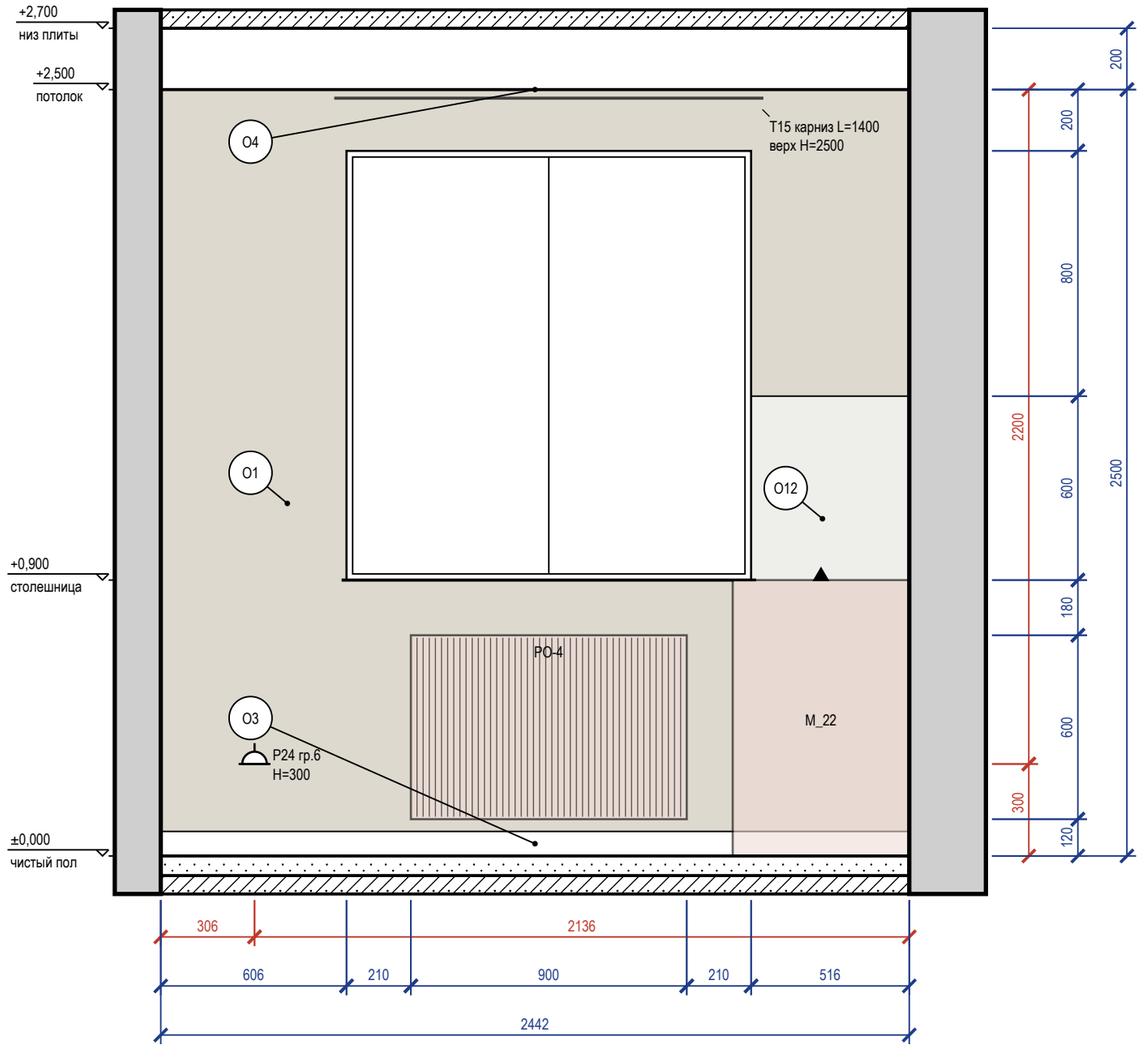


## Схема развёрток (М 1:100)

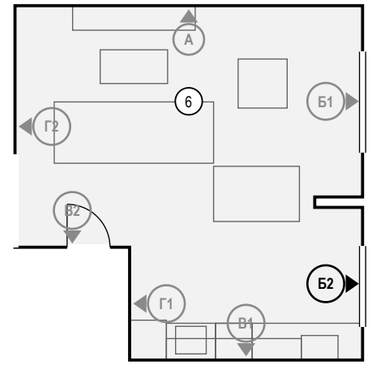


## Ведомость отделки (на листе)

| Марка | Поверхность | Материал, изделие | Цвет, код | Кол. |
|---|---|---|---|---|
| О1 | стены | окраска, Farrow & Ball Modern Emulsion, матовая, подготовка Q3 | Farrow & Ball No. 241 «Skimming Stone» | 3,9 м² |
| О3 | плинтус | плинтус МДФ, h 80 мм, аналог: плинтус МДФ под покраску 80×16 | Farrow & Ball No. 241 «Skimming Stone» | 2,4 м |
| О4 | потолок | окраска, Tikkurila Anti-Reflex 2, глубокоматовая, подготовка Q3 | Tikkurila V503 «Winter» | 29,2 м² |
| О12 | фартук | керамогранит, 1200×600×9 мм, аналог: керамогранит под травертин, матовый, затирка CG2WA | | 0,3 м² |

## Примечания

1. Размеры — в мм от чистовых поверхностей стен; условные обозначения и общие указания — лист 2.
2. Карнизы (шины) — по ведомости текстиля декоратора; длина L и верх H — по развёртке, крепление — до окраски потолка.
3. Высота фартука принята 600 мм над столешницей там, где нет навесных модулей и высота фартука не задана.
4. Выводы кухонной техники — по утверждённому проекту кухни: привязки выводов даются от осей модулей гарнитура.
5. Потолок на развёртках — по нижнему уровню У1; другие уровни потолка помещения: У2 +2,600.

| | | | | | |
|---|---|---|---|---|---|
| | | | | | Проект: Трёхкомнатная квартира |
| | Лист | № док. | Подпись | Дата | Развёртка стены Б2. Кухня-гостиная (пом. 6), кухонный |
| Дизайнер | Кырлан А.С. | | | 05.10.26 | |

| Стадия | Лист | Листов |
|---|---|---|
| П | 69 | 89 |

выпуск 05.10.2026 № 6a37468da7 · стр. 69 из 89

## Развёртка стены В1

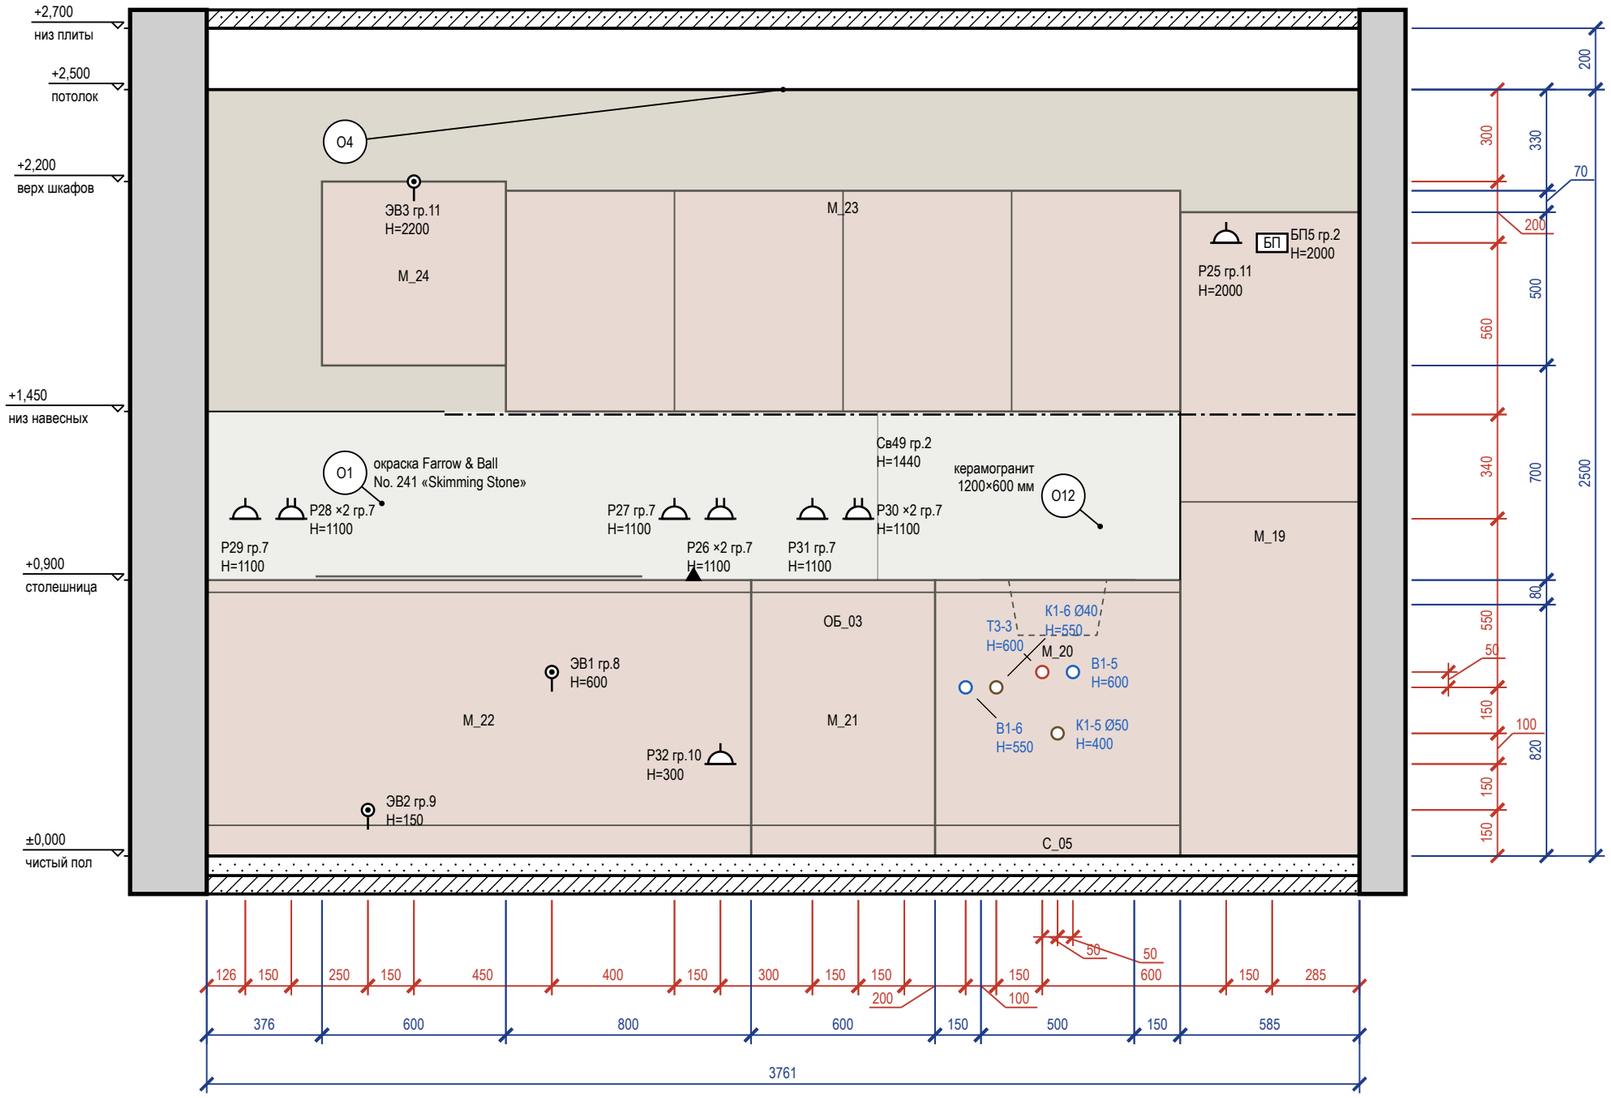


## Схема развёрток (М 1:100)

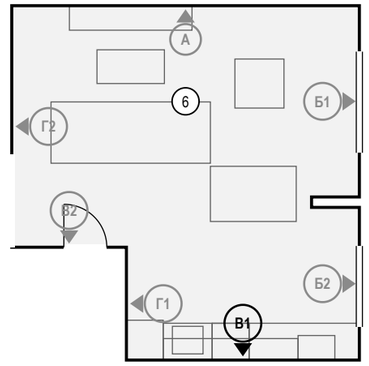


## Ведомость отделки (на листе)

| Марка | Поверхность | Материал, изделие | Цвет, код | Кол. |
|---|---|---|---|---|
| О1 | стены | окраска, Farrow & Ball Modern Emulsion, матовая, подготовка Q3 | Farrow & Ball No. 241 «Skimming Stone» | 7,7 м² |
| О4 | потолок | окраска, Tikkurila Anti-Reflex 2, глубокоматовая, подготовка Q3 | Tikkurila V503 «Winter» | 29,2 м² |
| О12 | фартук | керамогранит, 1200×600×9 мм, аналог: керамогранит под травертин, матовый, затирка CG2WA | | 1,7 м² |

Визуализация этой стены — лист 63

### Примечания

1. Размеры — в мм от чистовых поверхностей стен; условные обозначения и общие указания — лист 2.
2. Схема мебели, приборов и декора не является технической документацией для производства мебели; габариты — по паспортам изделий.
3. Выводы кухонной техники — по утверждённому проекту кухни: привязки выводов даются от осей модулей гарнитура.
4. Потолок на развёртках — по нижнему уровню У1; другие уровни потолка помещения: У2 +2,600.

| | | | | | |
|---|---|---|---|---|---|
| | | | | | Проект: Трёхкомнатная квартира |
| | Лист | № док. | Подпись | Дата | Развёртка стены В1. Кухня-гостиная (пом. 6), кухонный |
| Дизайнер | Кырлан А.С. | | | 05.10.26 | |

| Стадия | Лист | Листов |
|---|---|---|
| П | 70 | 89 |

выпуск 05.10.2026 № 6a37468da7 · стр. 70 из 89

## Развёртка стены А

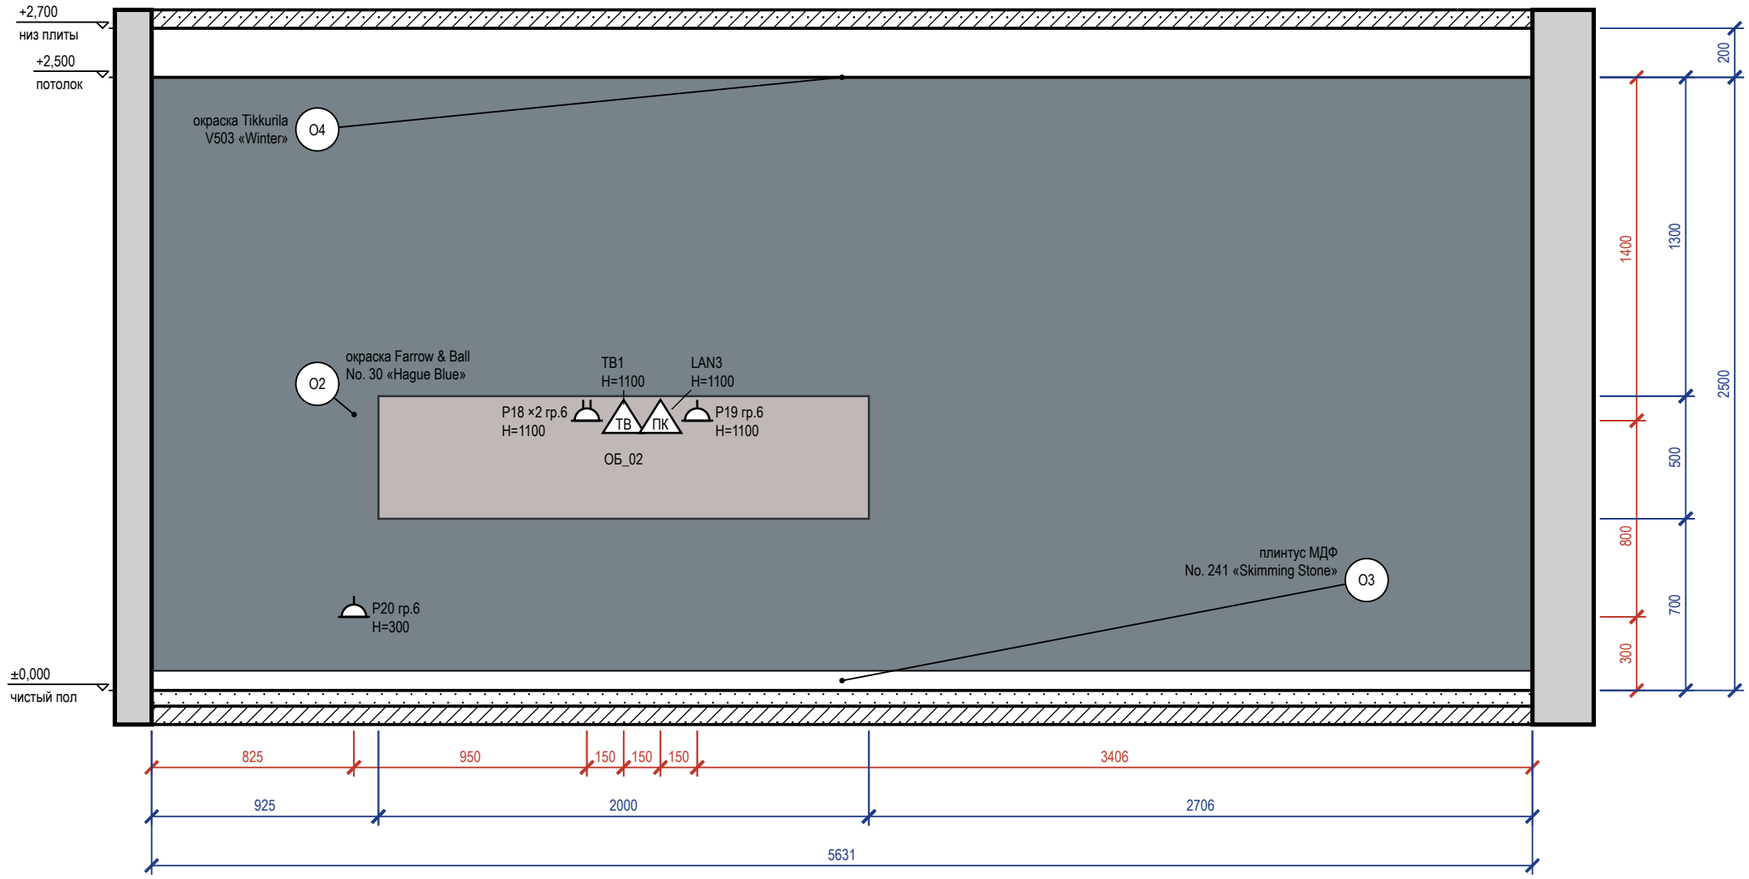


### Схема развёрток (М 1:100)

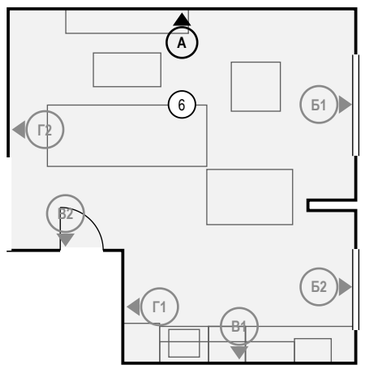


### Ведомость отделки (на листе)

| Марка | Поверхность | Материал, изделие | Цвет, код | Кол. |
|---|---|---|---|---|
| О2 | акцентная стена | окраска, Farrow & Ball Modern Emulsion, матовая, подготовка Q3 | Farrow & Ball No. 30 «Hague Blue» | 14,1 м² |
| О3 | плинтус | плинтус МДФ, h 80 мм, аналог: плинтус МДФ под покраску 80×16 | Farrow & Ball No. 241 «Skimming Stone» | 5,6 м |
| О4 | потолок | окраска, Tikkurila Anti-Reflex 2, глубокоматовая, подготовка Q3 | Tikkurila V503 «Winter» | 29,2 м² |

Визуализация этой стены — лист 64

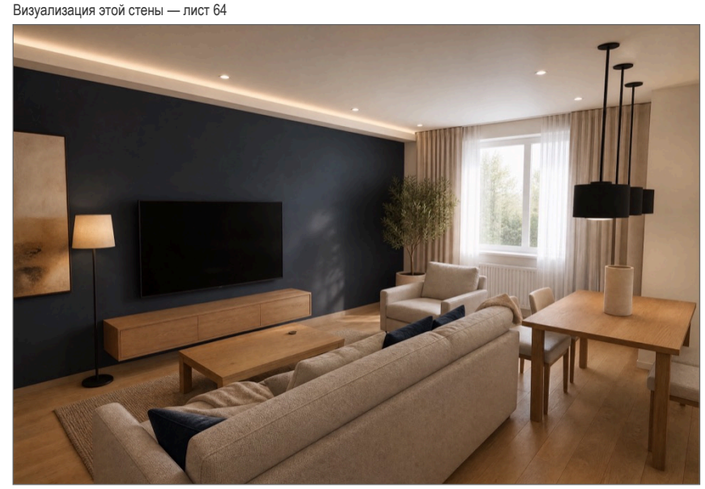

### Примечания

1. Размеры — в мм от чистовых поверхностей стен; условные обозначения и общие указания — лист 2.
2. Схема мебели, приборов и декора не является технической документацией для производства мебели; габариты — по паспортам изделий.
3. Потолок на развёртках — по нижнему уровню У1; другие уровни потолка помещения: У2 +2,600.

| | Лист | № док. | Подпись | Дата |
|---|---|---|---|---|
| Дизайнер | Кырлан А.С. | | | 05.10.26 |

Проект: Трёхкомнатная квартира

Развёртка стены А. Кухня-гостиная (пом. 6)

| Стадия | Лист | Листов |
|---|---|---|
| П | 71 | 89 |

выпуск 05.10.2026 № 6a37468da7 · стр. 71 из 89

## Развёртка стены Б1

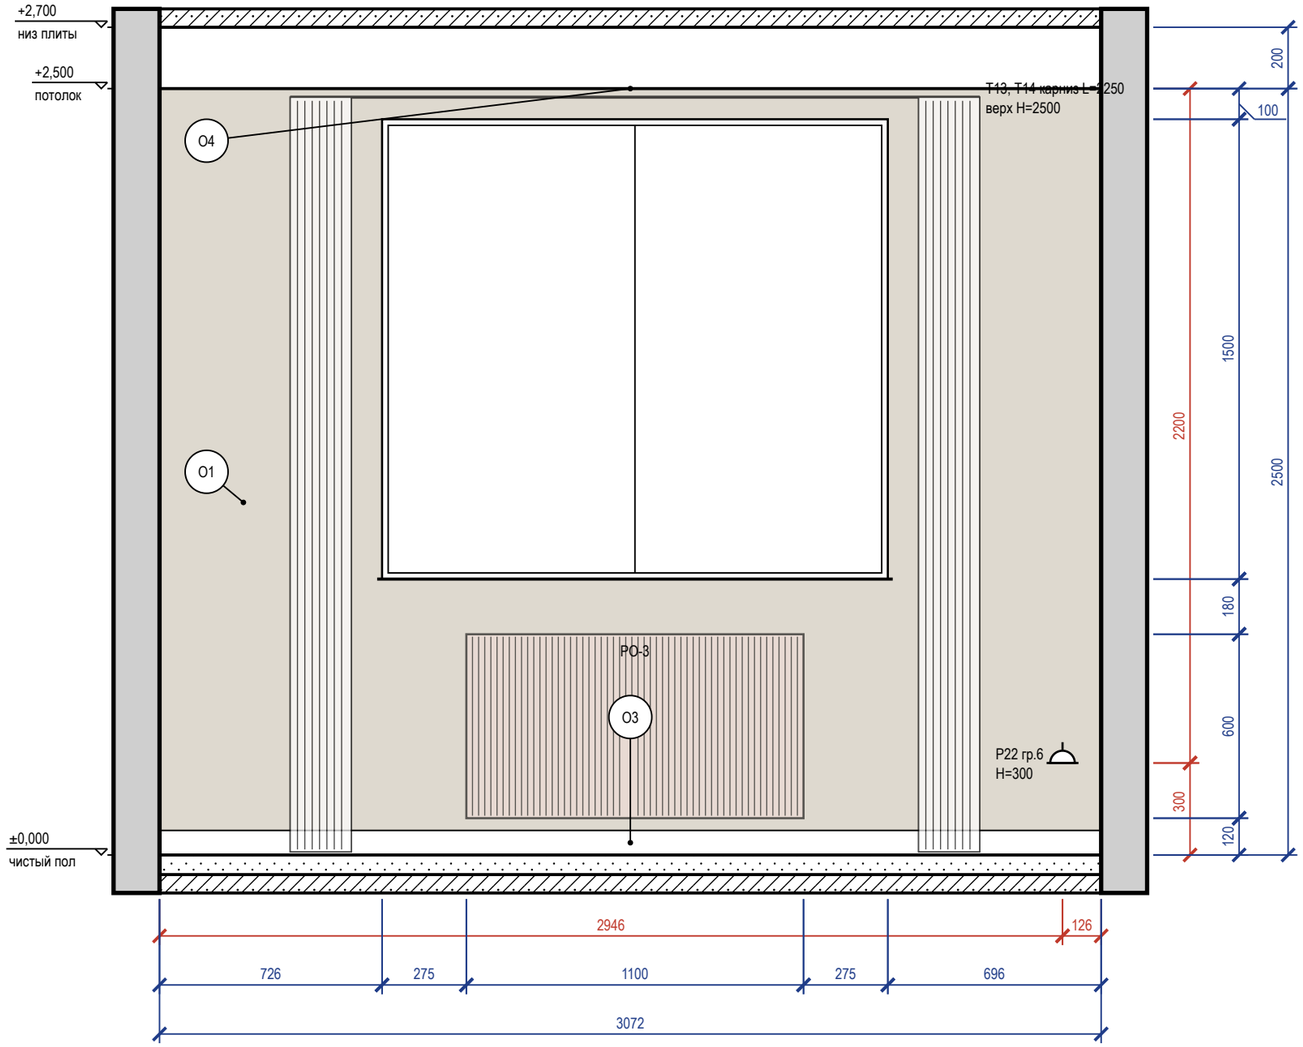


## Схема развёрток (М 1:100)

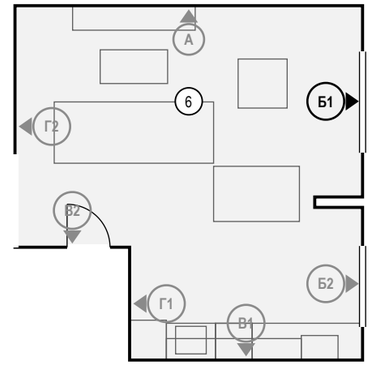


## Ведомость отделки (на листе)

| Марка | Поверхность | Материал, изделие | Цвет, код | Кол. |
|---|---|---|---|---|
| О1 | стены | окраска, Farrow & Ball Modern Emulsion, матовая, подготовка Q3 | Farrow & Ball No. 241 «Skimming Stone» | 5,2 м² |
| О3 | плинтус | плинтус МДФ, h 80 мм, аналог: плинтус МДФ под покраску 80×16 | Farrow & Ball No. 241 «Skimming Stone» | 3,1 м |
| О4 | потолок | окраска, Tikkurila Anti-Reflex 2, глубокоматовая, подготовка Q3 | Tikkurila V503 «Winter» | 29,2 м² |

Визуализация этой стены — лист 66

## Примечания

1. Размеры — в мм от чистовых поверхностей стен; условные обозначения и общие указания — лист 2.
2. Карнизы (шины) — по ведомости текстиля декоратора; длина L и верх H — по развёртке, крепление — до окраски потолка.
3. Потолок на развёртках — по нижнему уровню У1; другие уровни потолка помещения: У2 +2,600.
4. Линии узора (швы плитки, складки штор, рёбра радиаторов) прерываются у знаков и выносок — просвет между линиями не менее 0,7 мм.

| | | | | | |
|---|---|---|---|---|---|
| | | | | | Проект: Трёхкомнатная квартира |
| | Лист | № док. | Подпись | Дата | |
| Дизайнер | Кырлан А.С. | | | 05.10.26 | Развёртка стены Б1. Кухня-гостиная (пом. 6) |

| Стадия | Лист | Листов |
|---|---|---|
| П | 72 | 89 |

выпуск 05.10.2026 № 6a37468da7 · стр. 72 из 89

## Развёртка стены В2

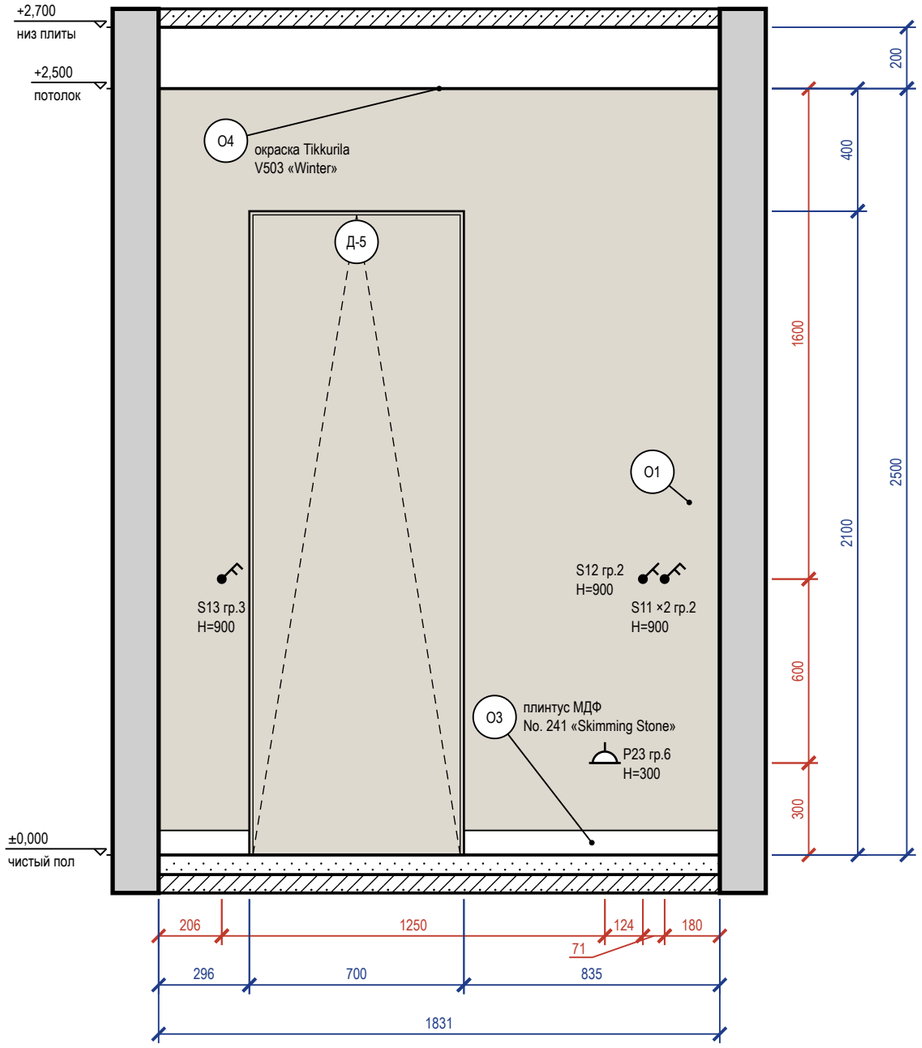


## Развёртка стены Г1

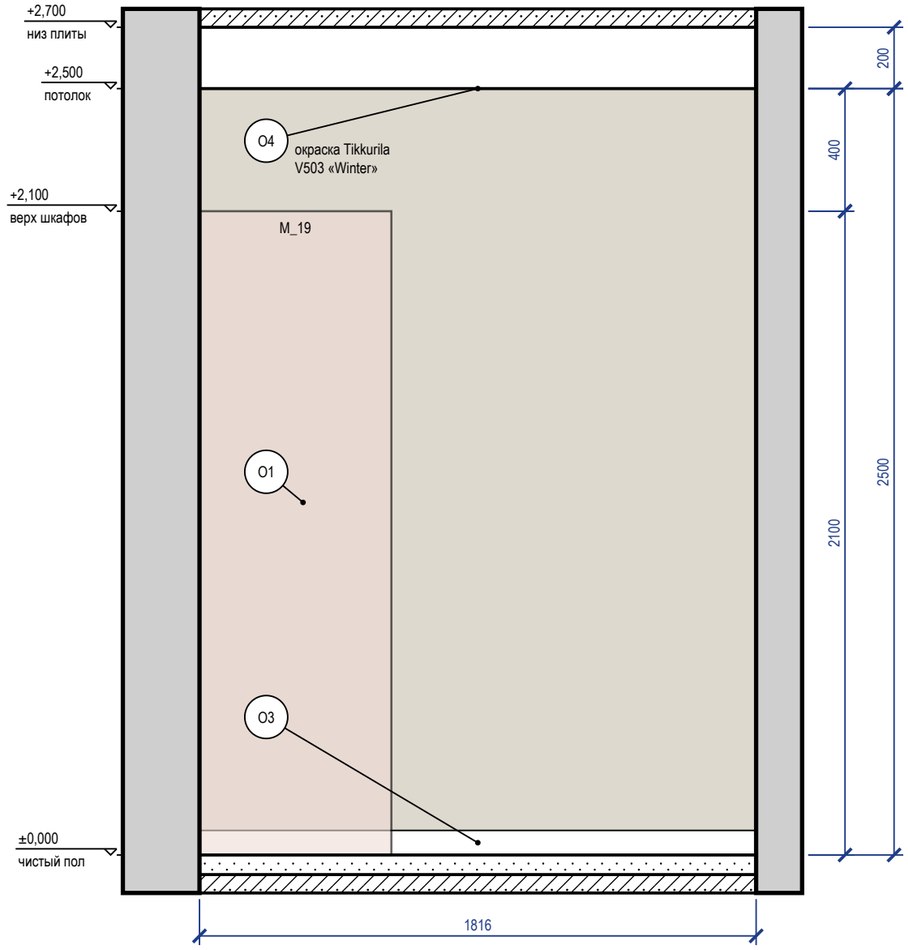


## Схема развёрток (М 1:100)

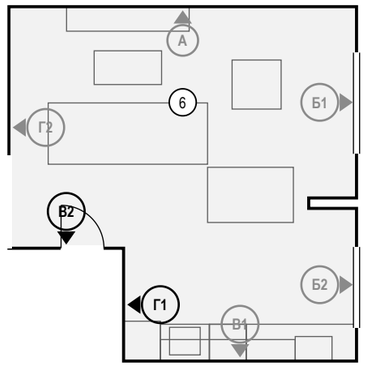


## Ведомость отделки (на листе)

| Марка | Поверхность | Материал, изделие | Цвет, код | Кол. |
|---|---|---|---|---|
| О1 | стены | окраска, Farrow & Ball Modern Emulsion, матовая, подготовка Q3 | Farrow & Ball No. 241 «Skimming Stone» | 7,6 м² |
| О3 | плинтус | плинтус МДФ, h 80 мм, аналог: плинтус МДФ под покраску 80×16 | Farrow & Ball No. 241 «Skimming Stone» | 2,9 м |
| О4 | потолок | окраска, Tikkurila Anti-Reflex 2, глубокоматовая, подготовка Q3 | Tikkurila V503 «Winter» | 29,2 м² |

Визуализация этой стены — лист 67

## Примечания

1. Размеры — в мм от чистовых поверхностей стен; условные обозначения и общие указания — лист 2.
2. Двери скрытого монтажа — полотно в плоскости стены, отделка стены по полотну, плинтус прерывается у короба (узел — на листе узлов).
3. Потолок на развёртках — по нижнему уровню У1; другие уровни потолка помещения: У2 +2,600.

| | | | | | |
|---|---|---|---|---|---|
| | | | | | Проект: Трёхкомнатная квартира |
| | Лист | № док. | Подпись | Дата | Развёртки стен В2, Г1. Кухня-гостиная (пом. 6) |
| Дизайнер | Кырлан А.С. | | | 05.10.26 | |

| Стадия | Лист | Листов |
|---|---|---|
| П | 73 | 89 |

выпуск 05.10.2026 № 6a37468da7 · стр. 73 из 89

## Развёртка стены Г2

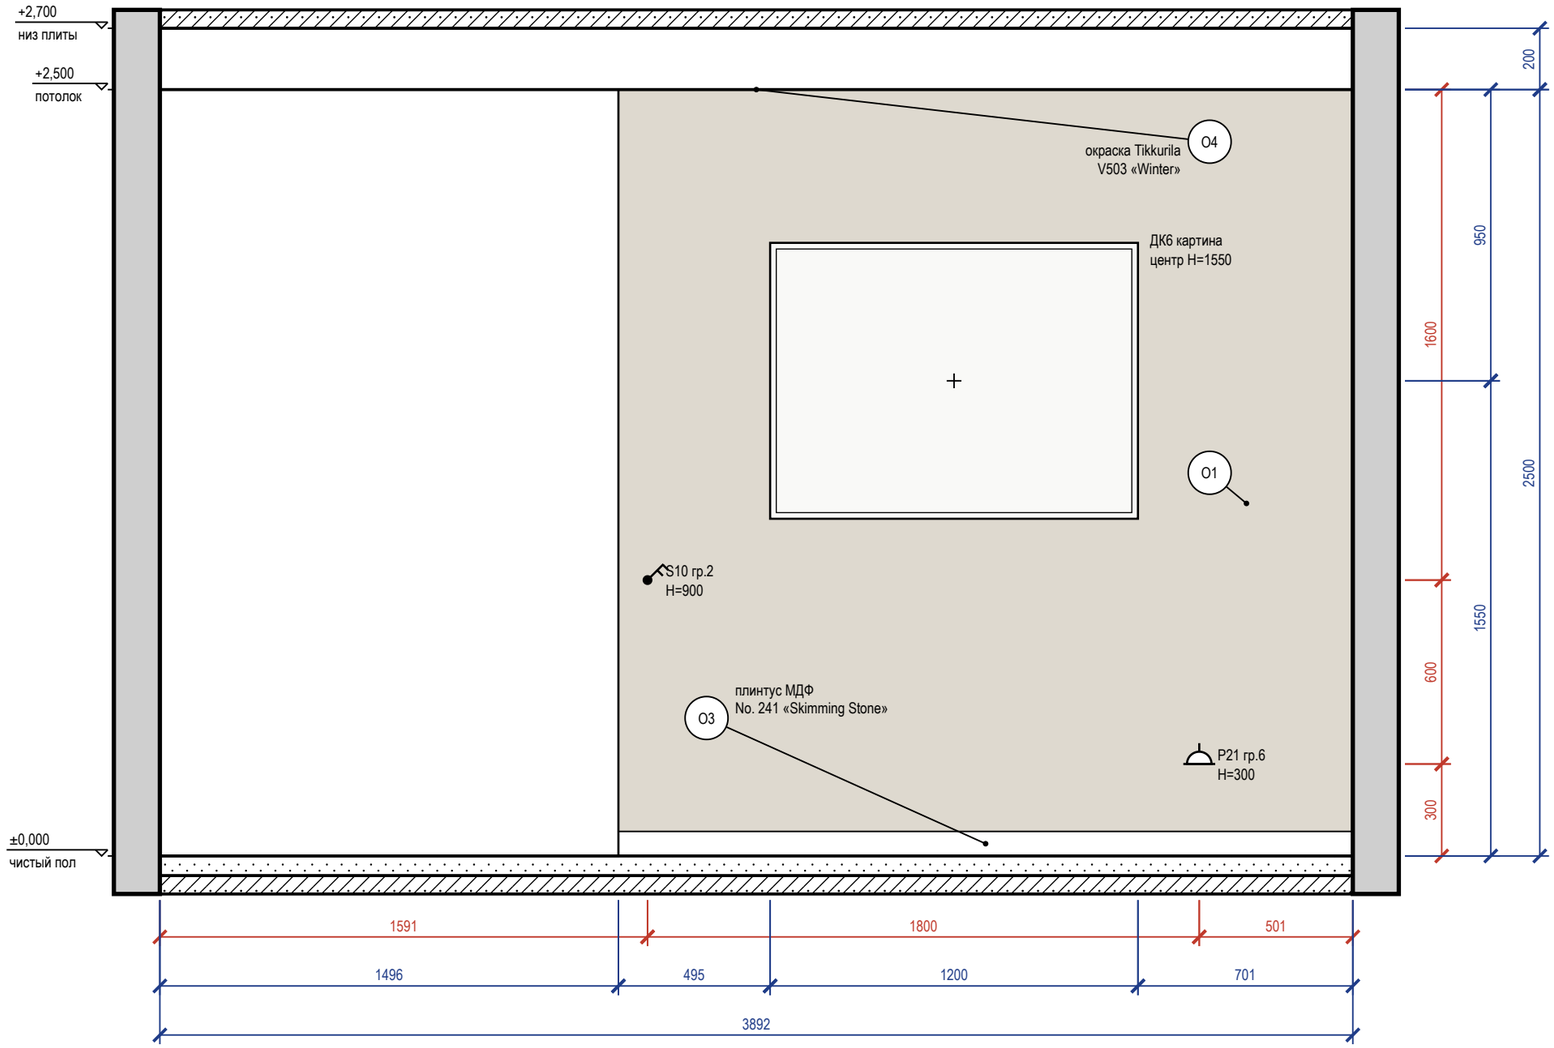


### Схема развёрток (М 1:100)

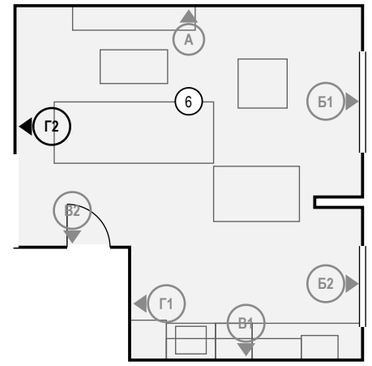


### Ведомость отделки (на листе)

| Марка | Поверхность | Материал, изделие | Цвет, код | Кол. |
|---|---|---|---|---|
| О1 | стены | окраска, Farrow & Ball Modern Emulsion, матовая, подготовка Q3 | Farrow & Ball No. 241 «Skimming Stone» | 6 м² |
| О3 | плинтус | плинтус МДФ, h 80 мм, аналог: плинтус МДФ под покраску 80×16 | Farrow & Ball No. 241 «Skimming Stone» | 2,4 м |
| О4 | потолок | окраска, Tikkurila Anti-Reflex 2, глубокоматовая, подготовка Q3 | Tikkurila V503 «Winter» | 29,2 м² |

Визуализация этой стены — лист 65

### Примечания

1. Размеры — в мм от чистовых поверхностей стен; условные обозначения и общие указания — лист 2.
2. Картины и зеркала крепить к основанию по паспорту изделия (закладные и анкеры — в перечне скрытых работ); крест — ось центра предмета.
3. Потолок на развёртках — по нижнему уровню У1; другие уровни потолка помещения: У2 +2,600.

| | | | | | |
|---|---|---|---|---|---|
| | | | | | Проект: Трёхкомнатная квартира |
| | Лист | № док. | Подпись | Дата | Развёртка стены Г2. Кухня-гостиная (пом. 6) |
| Дизайнер | Кырлан А.С. | | | 05.10.26 | |

| Стадия | Лист | Листов |
|---|---|---|
| П | 74 | 89 |

выпуск 05.10.2026 № 6a37468da7 · стр. 74 из 89

| | | | | | |
|---|---|---|---|---|---|
| | | | | | Проект: Трёхкомнатная квартира |
| | Лист | № док. | Подпись | Дата | |
| Дизайнер | Кырлан А.С. | | | 05.10.26 | Визуализация: Санузел 2 |

| Стадия | Лист | Листов |
|---|---|---|
| П | 75 | 89 |

выпуск 05.10.2026 № 6a37468da7 · стр. 75 из 89

| | | | | | |
|---|---|---|---|---|---|
| | | | | | Проект: Трёхкомнатная квартира |
| | Лист | № док. | Подпись | Дата | |
| Дизайнер | Кырлан А.С. | | | 05.10.26 | Визуализация: Санузел 2 |

| Стадия | Лист | Листов |
|---|---|---|
| П | 76 | 89 |

выпуск 05.10.2026 № 6a37468da7 · стр. 76 из 89

## Развёртка стены А

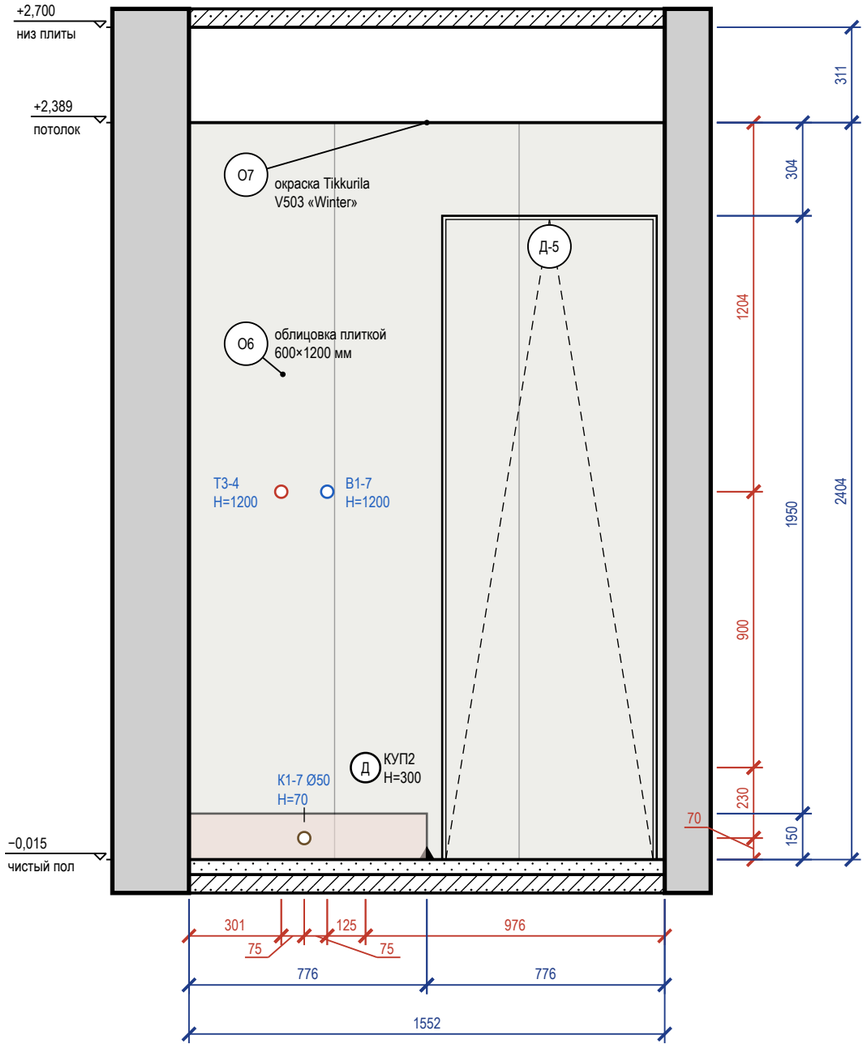


## Развёртка стены Б

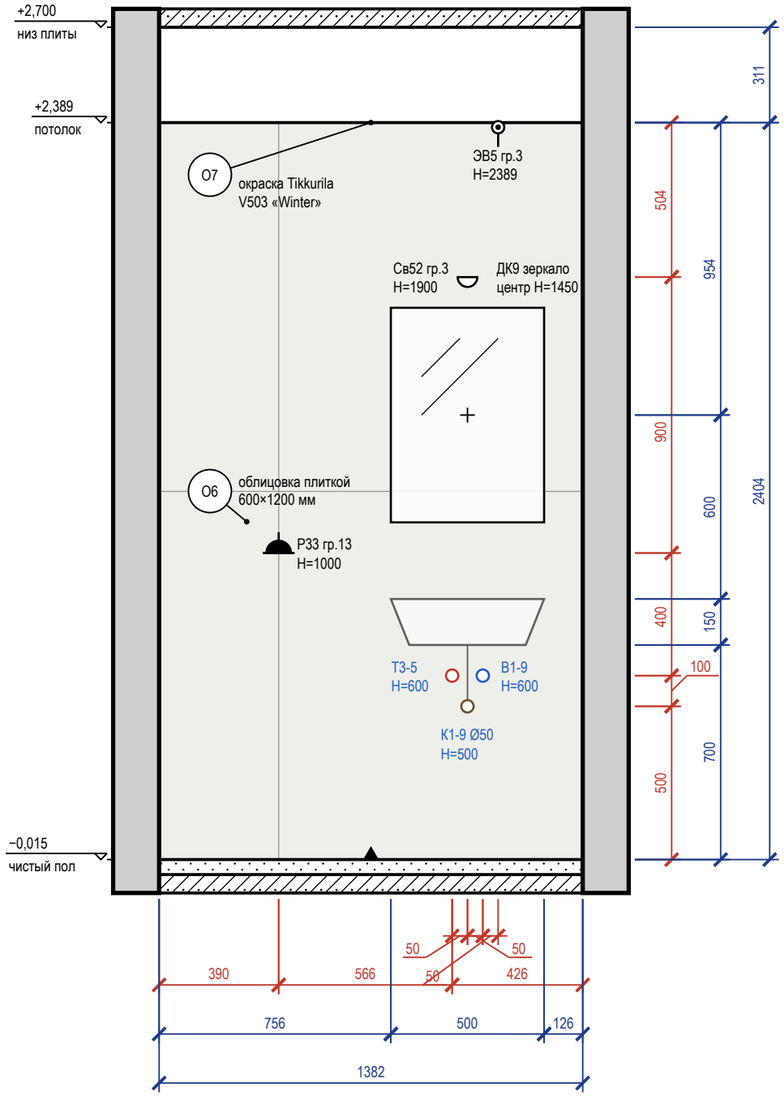


Визуализация этой стены — лист 75

### Схема развёрток (М 1:100)

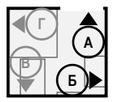


### Ведомость отделки (на листе)

| Марка | Поверхность | Материал, изделие | Цвет, код | Кол. |
|---|---|---|---|---|
| О6 | стены | облицовка плиткой, 600×1200×9 мм, аналог: керамогранит под травертин, матовый, затирка CG2WA | | 5,6 м² |
| О7 | потолок | окраска, Tikkurila Luja 7, матовая, подготовка Q3 | Tikkurila V503 «Winter» | 2,3 м² |

### Примечания

1. Размеры — в мм от чистовых поверхностей стен; условные обозначения и общие указания — лист 2.
2. Схема мебели, приборов и декора не является технической документацией для производства мебели; габариты — по паспортам изделий.
3. Выводы ВК — коды и высоты по листу выводов сантехники.
4. Облицовка — по сетке швов 2 мм, раскладка от оси стены (треугольник у пола), целые ряды от пола; подрезки — по листу раскладки плитки.
5. Гидроизоляция в 2 слоя, заход на стены 200 мм — до облицовки, с актом скрытых работ и тестом проливом (узел — на листе узлов).
6. Картины и зеркала крепить к основанию по паспорту изделия (закладные и анкеры — в перечне скрытых работ); крест — ось центра предмета.
7. Двери скрытого монтажа — полотно в плоскости стены, отделка стены по полотну, плинтус прерывается у короба (узел — на листе узлов).

| | | | | | |
|---|---|---|---|---|---|
| | | | | | Проект: Трёхкомнатная квартира |
| | Лист | № док. | Подпись | Дата | |
| Дизайнер | Кырлан А.С. | | | 05.10.26 | Развёртки стен А, Б. Санузел 2 (пом. 7) |

| Стадия | Лист | Листов |
|---|---|---|
| П | 77 | 89 |

выпуск 05.10.2026 № 6a37468da7 · стр. 77 из 89

## Развёртка стены В

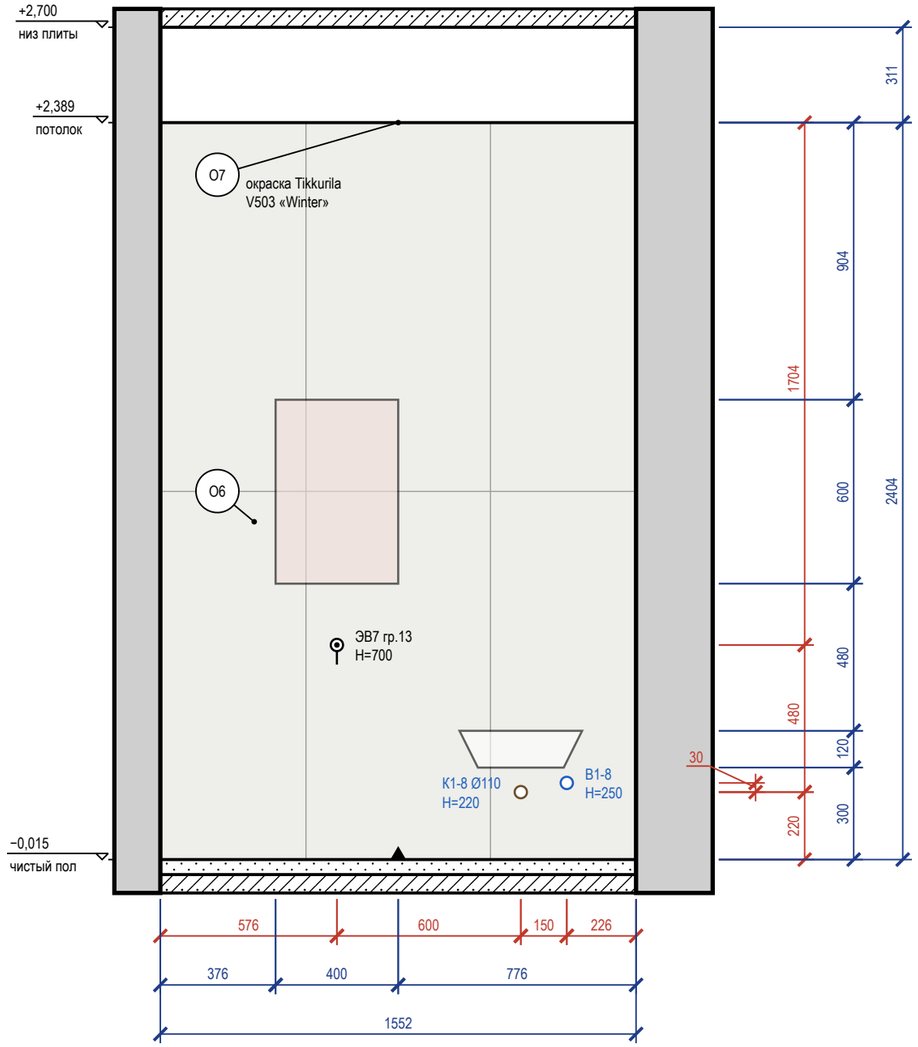


## Развёртка стены Г

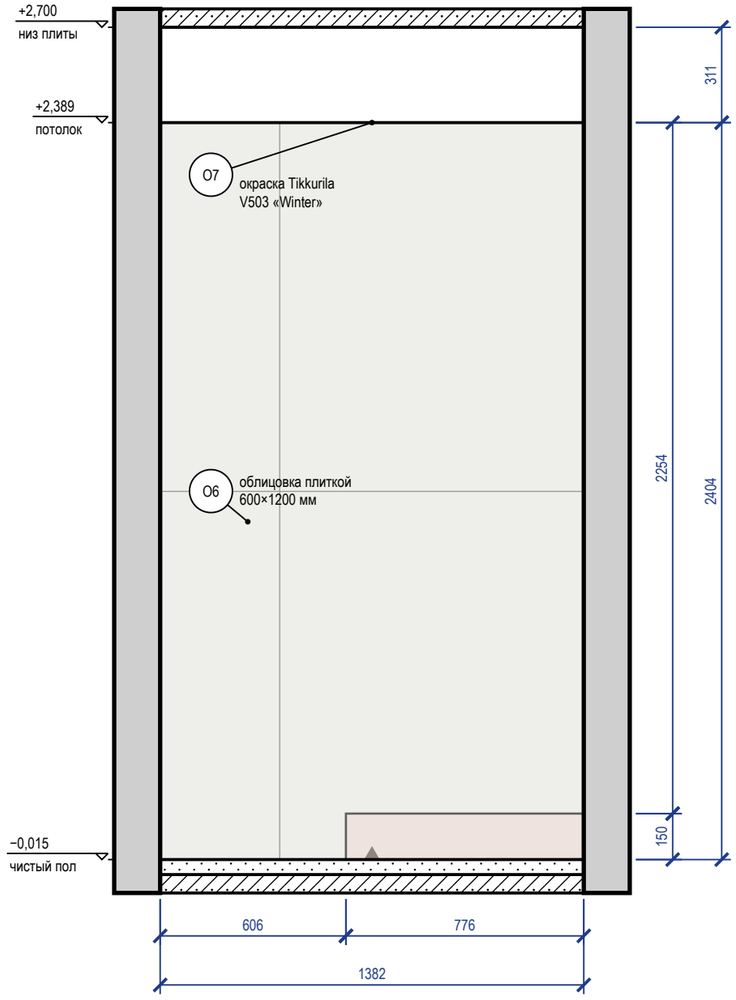


Визуализация этой стены — лист 76

### Схема развёрток (М 1:100)

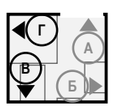


### Ведомость отделки (на листе)

| Марка | Поверхность | Материал, изделие | Цвет, код | Кол. |
|---|---|---|---|---|
| О6 | стены | облицовка плиткой, 600×1200×9 мм, аналог: керамогранит под травертин, матовый, затирка CG2WA | | 7,1 м² |
| О7 | потолок | окраска, Tikkurila Luja 7, матовая, подготовка Q3 | Tikkurila V503 «Winter» | 2,3 м² |

### Примечания

1. Размеры — в мм от чистовых поверхностей стен; условные обозначения и общие указания — лист 2.
2. Схема мебели, приборов и декора не является технической документацией для производства мебели; габариты — по паспортам изделий.
3. Выводы ВК — коды и высоты по листу выводов сантехники.
4. Облицовка — по сетке швов 2 мм, раскладка от оси стены (треугольник у пола), целые ряды от пола; подрезки — по листу раскладки плитки.
5. Гидроизоляция в 2 слоя, заход на стены 200 мм — до облицовки, с актом скрытых работ и тестом проливом (узел — на листе узлов).

| | | | | | |
|---|---|---|---|---|---|
| | | | | | Проект: Трёхкомнатная квартира |
| | Лист | № док. | Подпись | Дата | Развёртки стен В, Г. Санузел 2 (пом. 7) |
| Дизайнер | Кырлан А.С. | | | 05.10.26 | |

| Стадия | Лист | Листов |
|---|---|---|
| П | 78 | 89 |

выпуск 05.10.2026 № 6a37468da7 · стр. 78 из 89

| | | | | | |
|---|---|---|---|---|---|
| | | | | | Проект: Трёхкомнатная квартира |
| | Лист | № док. | Подпись | Дата | |
| Дизайнер | Кырлан А.С. | | | 05.10.26 | Визуализация коридора |

| Стадия | Лист | Листов |
|---|---|---|
| П | 79 | 89 |

выпуск 05.10.2026 № 6a37468da7 · стр. 79 из 89

| | | | | | |
|---|---|---|---|---|---|
| | | | | | Проект: Трёхкомнатная квартира |
| | Лист | № док. | Подпись | Дата | Визуализация коридора |
| Дизайнер | Кырлан А.С. | | | 05.10.26 | |

| Стадия | Лист | Листов |
|---|---|---|
| П | 80 | 89 |

выпуск 05.10.2026 № 6a37468da7 · стр. 80 из 89

## Развёртка стены А

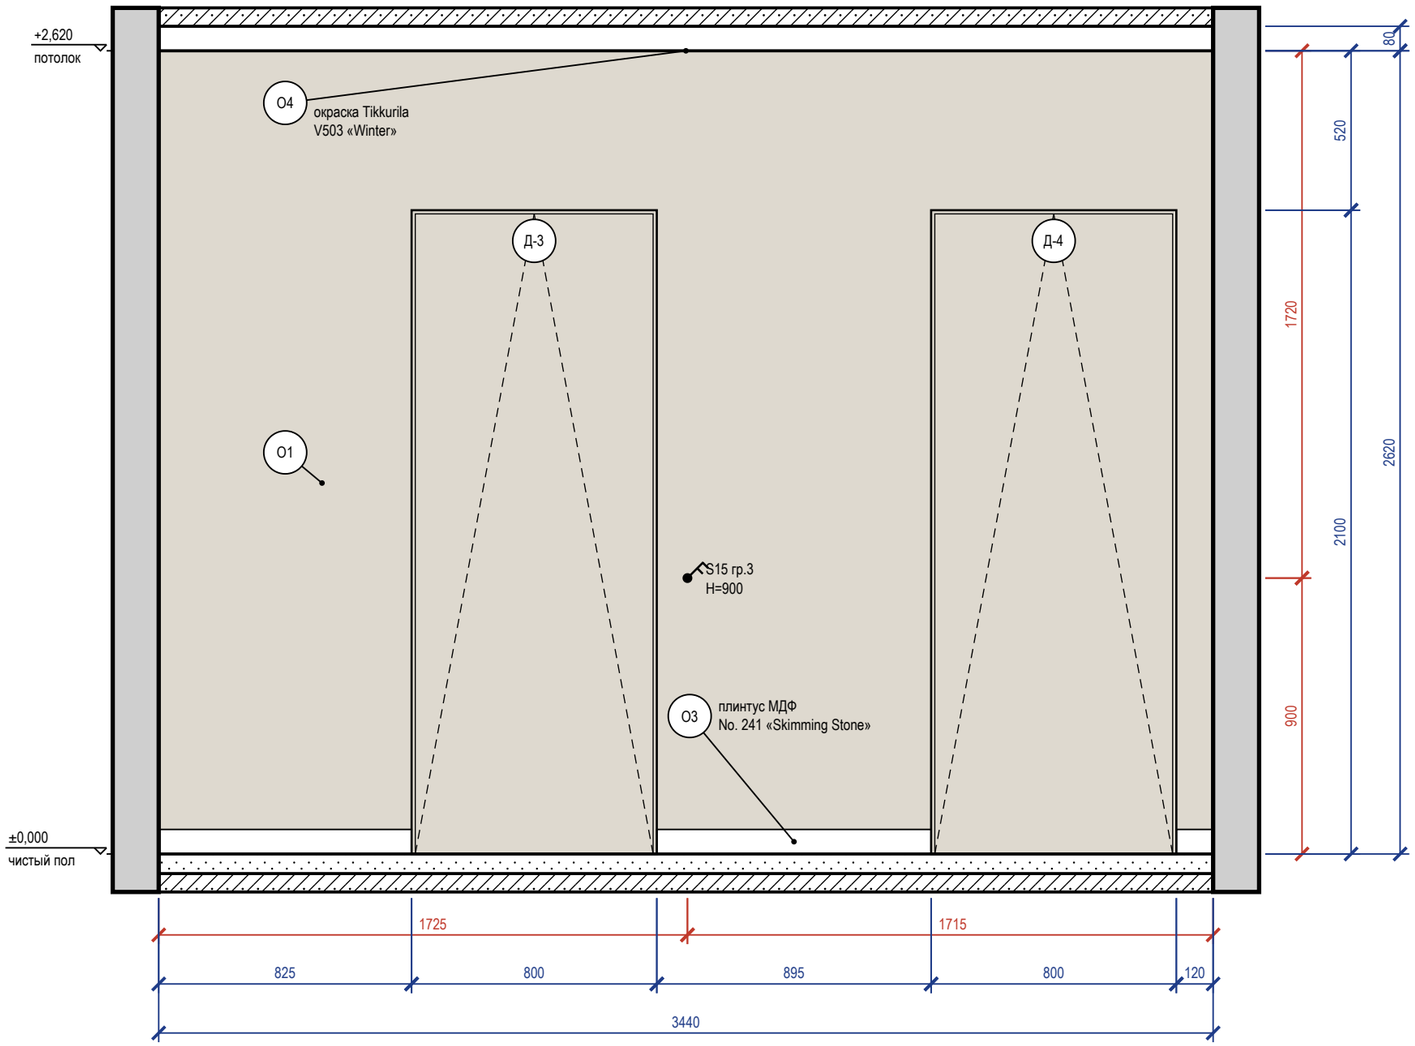


## Развёртка стены Б

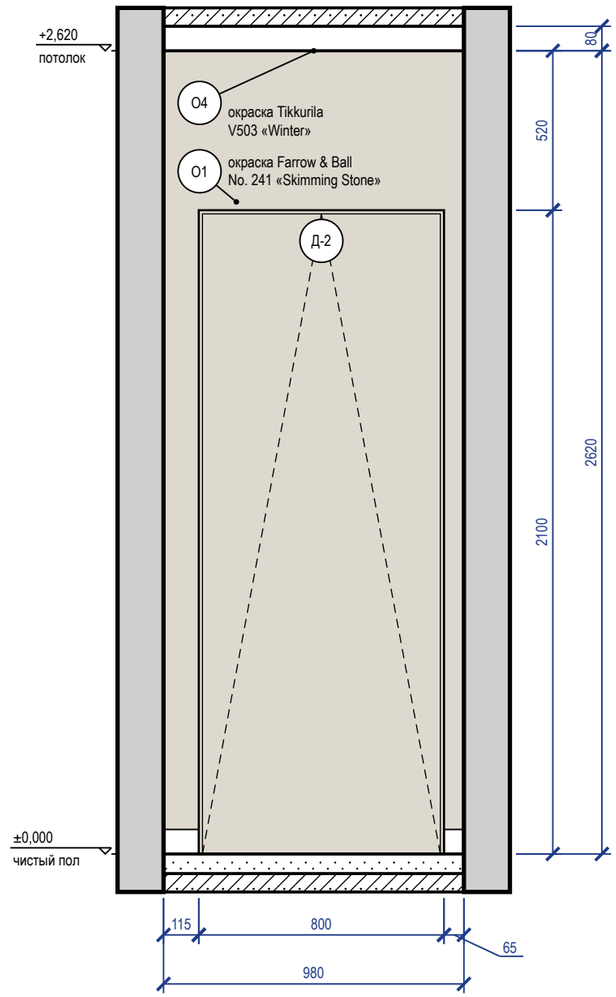


### Схема развёрток (М 1:100)

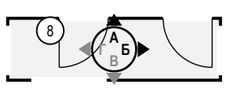


### Ведомость отделки (на листе)

| Марка | Поверхность | Материал, изделие | Цвет, код | Кол. |
|---|---|---|---|---|
| О1 | стены | окраска, Farrow & Ball Modern Emulsion, матовая, подготовка Q3 | Farrow & Ball No. 241 «Skimming Stone» | 6,5 м² |
| О3 | плинтус | плинтус МДФ, h 80 мм, аналог: плинтус МДФ под покраску 80×16 | Farrow & Ball No. 241 «Skimming Stone» | 2 м |
| О4 | потолок | окраска, Tikkurila Anti-Reflex 2, глубокоматовая, подготовка Q3 | Tikkurila V503 «Winter» | 3,5 м² |

Визуализация этой стены — лист 79

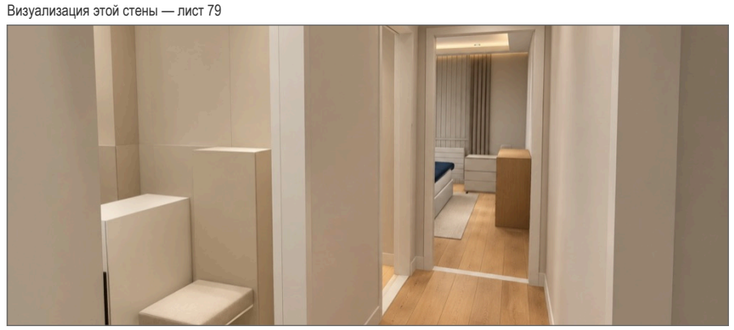

### Примечания

1. Размеры — в мм от чистовых поверхностей стен; условные обозначения и общие указания — лист 2.
2. Двери скрытого монтажа — полотно в плоскости стены, отделка стены по полотну, плинтус прерывается у короба (узел — на листе узлов).

| | | | | | |
|---|---|---|---|---|---|
| | | | | | Проект: Трёхкомнатная квартира |
| | Лист | № док. | Подпись | Дата | Развёртки стен А, Б. Коридор (пом. 8) |
| Дизайнер | Кырлан А.С. | | | 05.10.26 | |

| Стадия | Лист | Листов |
|---|---|---|
| П | 81 | 89 |

выпуск 05.10.2026 № 6a37468da7 · стр. 81 из 89

## Развёртка стены В

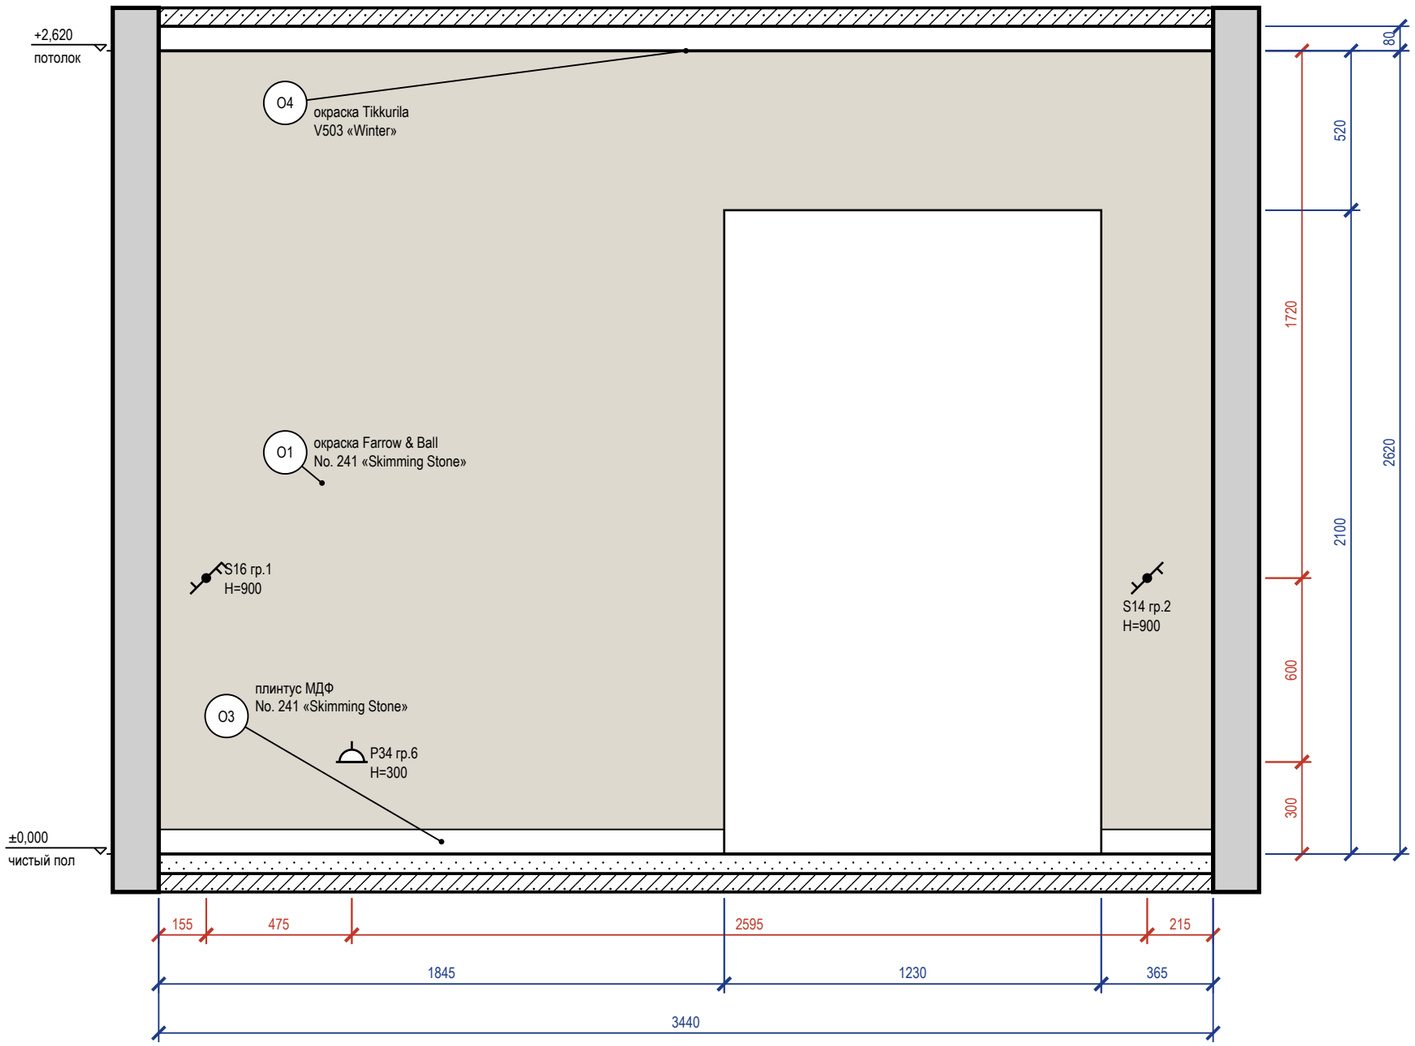


## Развёртка стены Г

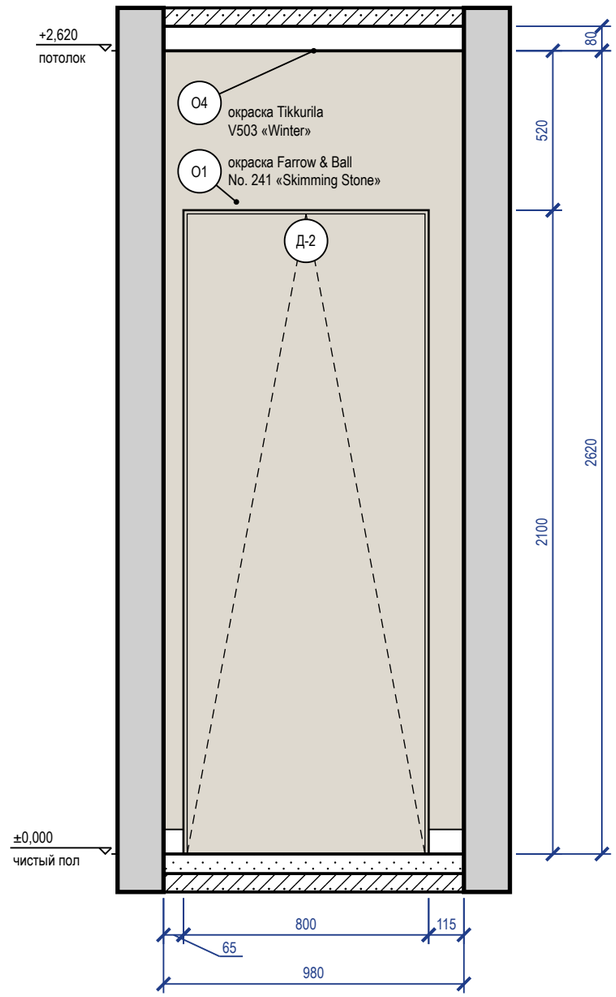


### Схема развёрток (М 1:100)

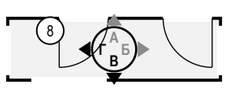


### Ведомость отделки (на листе)

| Марка | Поверхность | Материал, изделие | Цвет, код | Кол. |
|---|---|---|---|---|
| О1 | стены | окраска, Farrow & Ball Modern Emulsion, матовая, подготовка Q3 | Farrow & Ball No. 241 «Skimming Stone» | 7,3 м² |
| О3 | плинтус | плинтус МДФ, h 80 мм, аналог: плинтус МДФ под покраску 80×16 | Farrow & Ball No. 241 «Skimming Stone» | 2,4 м |
| О4 | потолок | окраска, Tikkurila Anti-Reflex 2, глубокоматовая, подготовка Q3 | Tikkurila V503 «Winter» | 3,5 м² |

Визуализация этой стены — лист 80

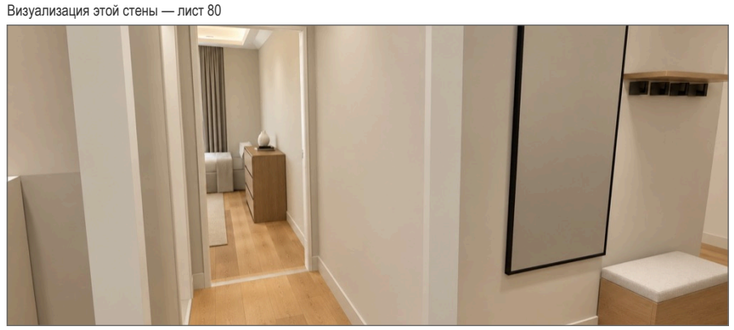

### Примечания

1. Размеры — в мм от чистовых поверхностей стен; условные обозначения и общие указания — лист 2.
2. Двери скрытого монтажа — полотно в плоскости стены, отделка стены по полотну, плинтус прерывается у короба (узел — на листе узлов).

| | | | | |
|---|---|---|---|---|
| | Лист | № док. | Подпись | Дата |
| Дизайнер | Кырлан А.С. | | | 05.10.26 |

Проект: Трёхкомнатная квартира

Развёртки стен В, Г. Коридор (пом. 8)

| Стадия | Лист | Листов |
|---|---|---|
| П | 82 | 89 |

выпуск 05.10.2026 № 6a37468da7 · стр. 82 из 89

## Вид с фасадами

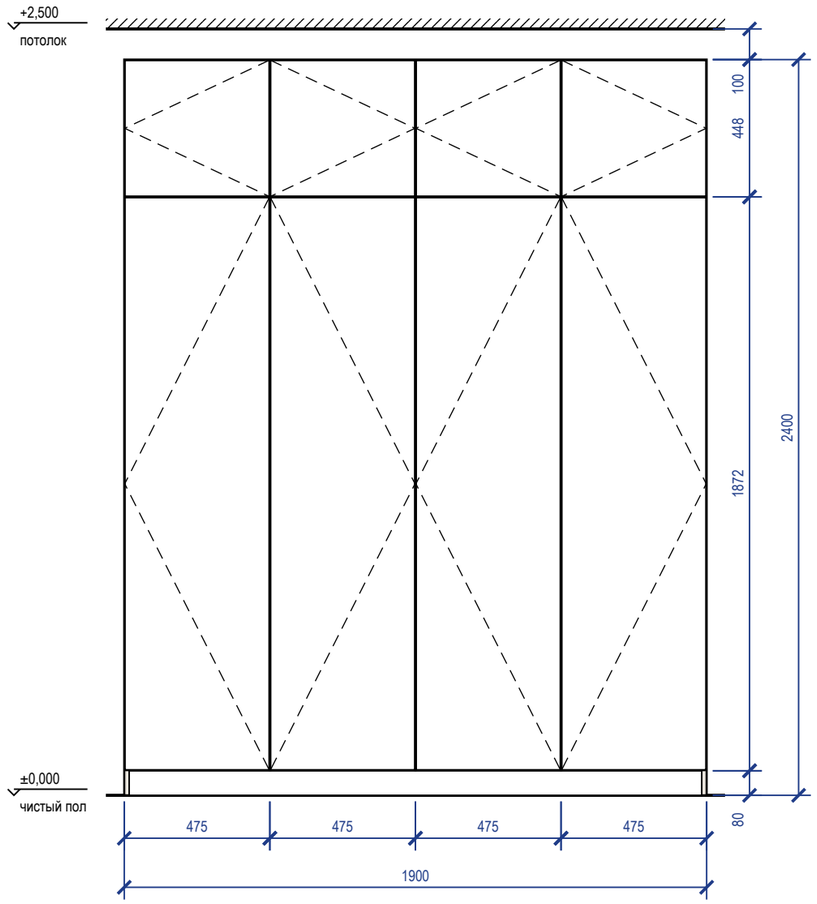


## Вид без фасадов

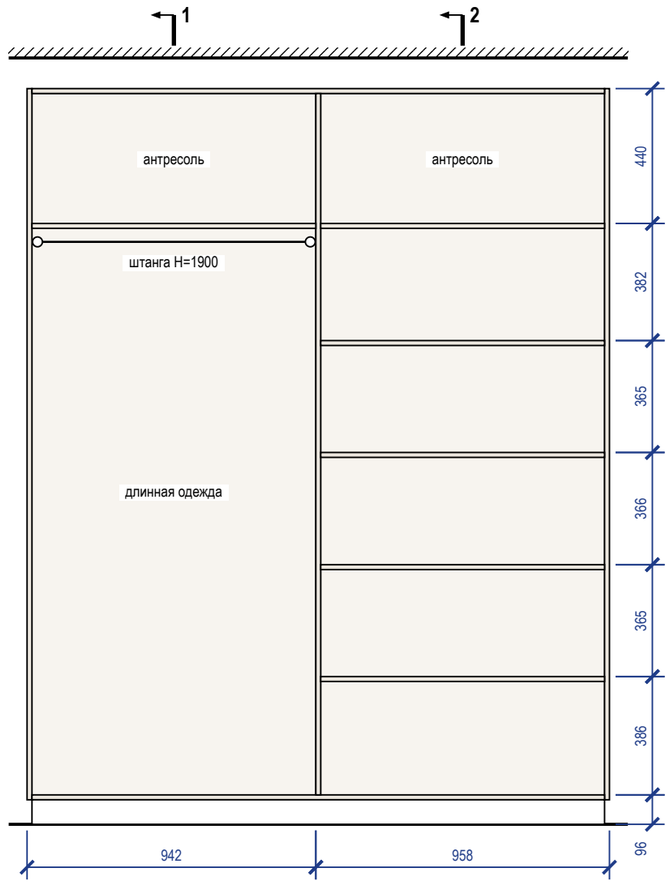


## Разрез 1-1

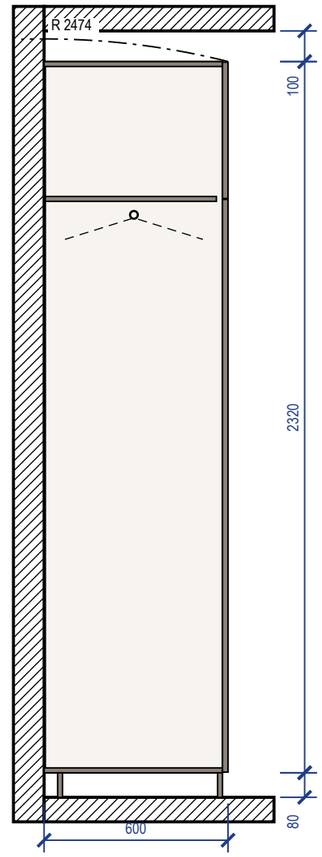


## Разрез 2-2

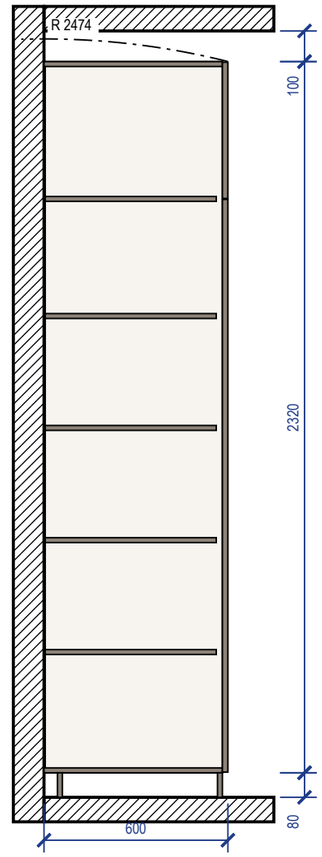


### Примечания

1. Размеры — в мм по чистовой отделке; изделие 1900×600×2400 (Ш×Г×В). Перед раскроем — контрольный замер цеха после чистовой отделки стен, пола и потолка.
2. Корпус — ЛДСП 16 мм, задняя стенка ХДФ 4 мм в паз, цоколь 80 мм на регулируемых опорах; фасады — МДФ, эмаль матовая 18 мм накладные, цвет — по колерной карте; петли с доводчиком: фасад 1869 мм — 4 петли, фасад 445 мм — 2 петли.
3. Кромка: скрытые торцы 0,4 мм, видимые 2 мм (ПВХ/АБС).
4. Номинальные зазоры: между фасадами 3 мм, фасад — стена и фасад — потолок не менее 3 мм, фасад ящика — стойка 2 мм.
5. Ящики — направляющие полного выдвижения NL 550 (внутренняя глубина 578 мм ≥ NL + 3); присадка по 32-й системе — выполняет цех.
6. Зазор до потолка 100 мм — закрыть планкой в цвет корпуса при монтаже.
7. Подъём корпуса: диагональ боковины $\sqrt{(2400^2 + 600^2)} = 2474$ мм < 2500 мм до потолка — корпус собирается лёжа и поднимается поворотом.
8. Крепление к стене от опрокидывания: уголок к стене, 2 шт.; основание стены и шаг анкеров — монтажная схема шкафов.

## 3D орто

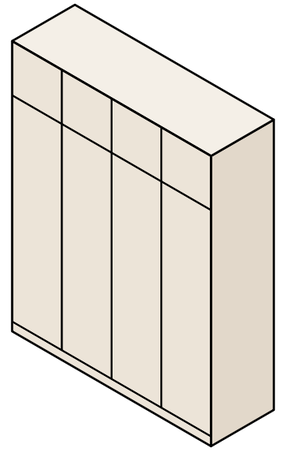

| | | | | | | | |
|---|---|---|---|---|---|---|---|
| | | | | | Проект: Трёхкомнатная квартира | | |
| | Лист | № док. | Подпись | Дата | | | |
| Дизайнер | Кырлан А.С. | | | 05.10.26 | Шкаф распашной M_05 | Стадия | Лист | Листов |
| | | | | | | П | Д_1 | 89 |

выпуск 05.10.2026 № 6a37468da7 · стр. 83 из 89

## Общий вид

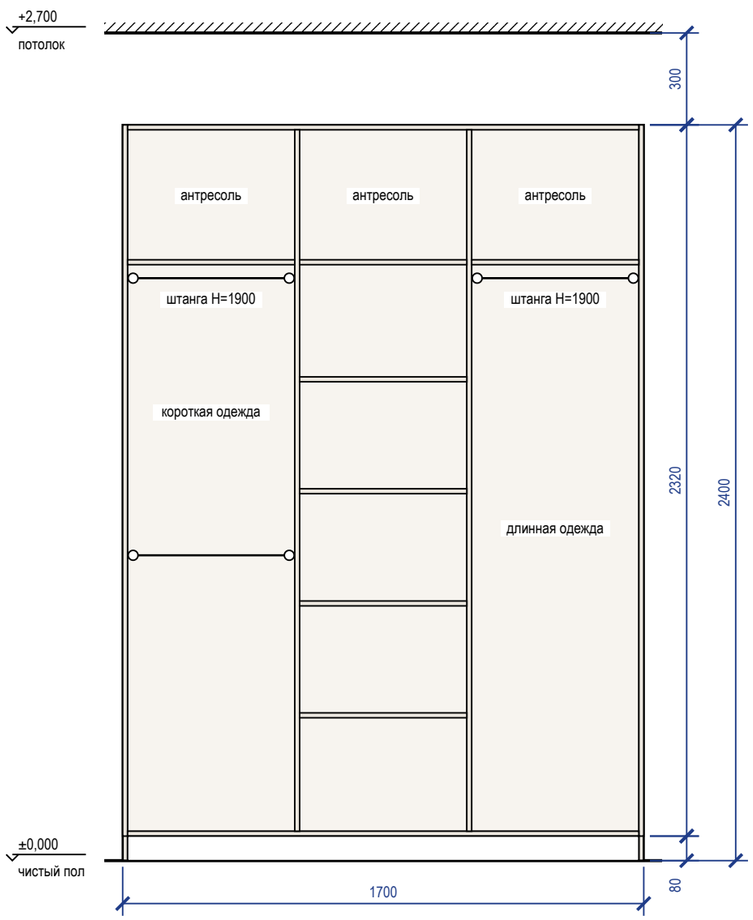


## Наполнение, размеры в свету

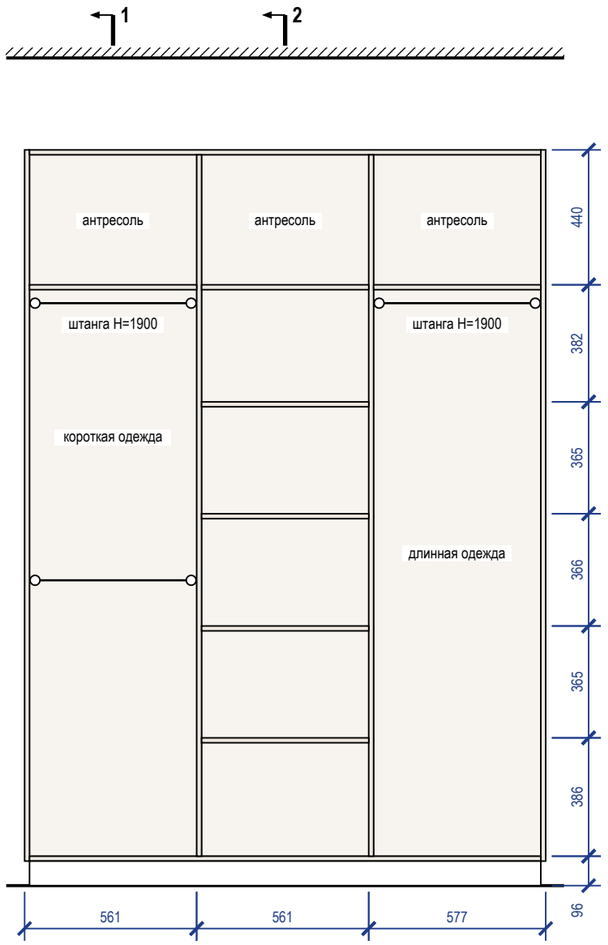


## Разрез 1-1

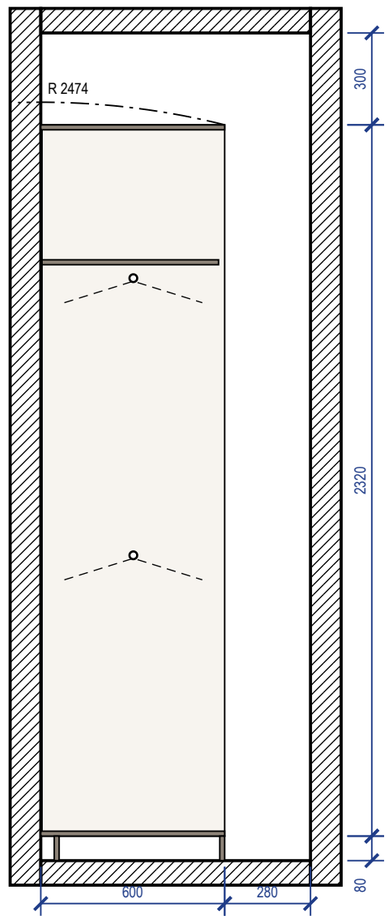


## Разрез 2-2

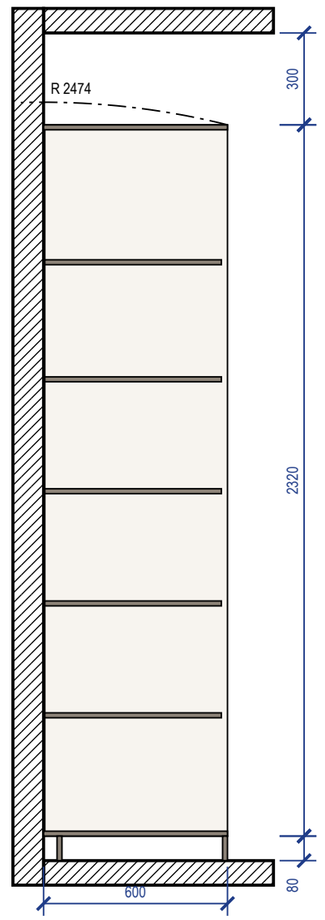


### Примечания

1. Размеры — в мм по чистовой отделке; изделие 1700×600×2400 (Ш×Г×В). Перед раскроем — контрольный замер цеха после чистовой отделки стен, пола и потолка.
2. Корпус — ЛДСП 16 мм, задняя стенка ХДФ 4 мм в паз, цоколь 80 мм на регулируемых опорах; открытая система без фасадов, ящики с фасадами.
3. Кромка: скрытые торцы 0,4 мм, видимые 2 мм (ПВХ/АБС).
4. Номинальные зазоры: между фасадами ящиков 3 мм, фасад ящика — стойка 2 мм.
5. Ящики — направляющие полного выдвижения NL 550 (внутренняя глубина 596 мм ≥ NL + 3); присадка по 32-й системе — выполняет цех.
6. Зазор до потолка 300 мм.
7. Подъём корпуса: диагональ боковины $\sqrt{(2400^2 + 600^2)} = 2474$ мм < 2700 мм до потолка — корпус собирается лёжа и поднимается поворотом.
8. Крепление к стене от опрокидывания: крепление к стене, 3 точки; основание стены и шаг анкеров — монтажная схема шкафов.
9. Проход перед изделием 280 мм показан на разрезе 1-1: меньше 600 мм — глубину уменьшить (торцевые штанги при глубине 350–450 мм) или изменить расстановку.

## 3D орто

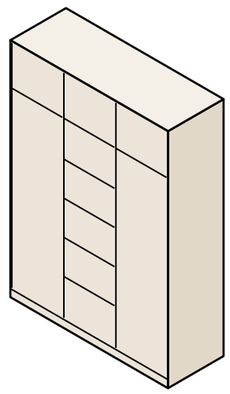

| | | | | | |
|---|---|---|---|---|---|
| | | | | | Проект: Трёхкомнатная квартира |
| | Лист | № док. | Подпись | Дата | |
| Дизайнер | Кырлан А.С. | | | 05.10.26 | Система хранения M_07 |

| Стадия | Лист | Листов |
|---|---|---|
| П | Д_2 | 89 |

выпуск 05.10.2026 № 6a37468da7 · стр. 84 из 89

## Вид с фасадами

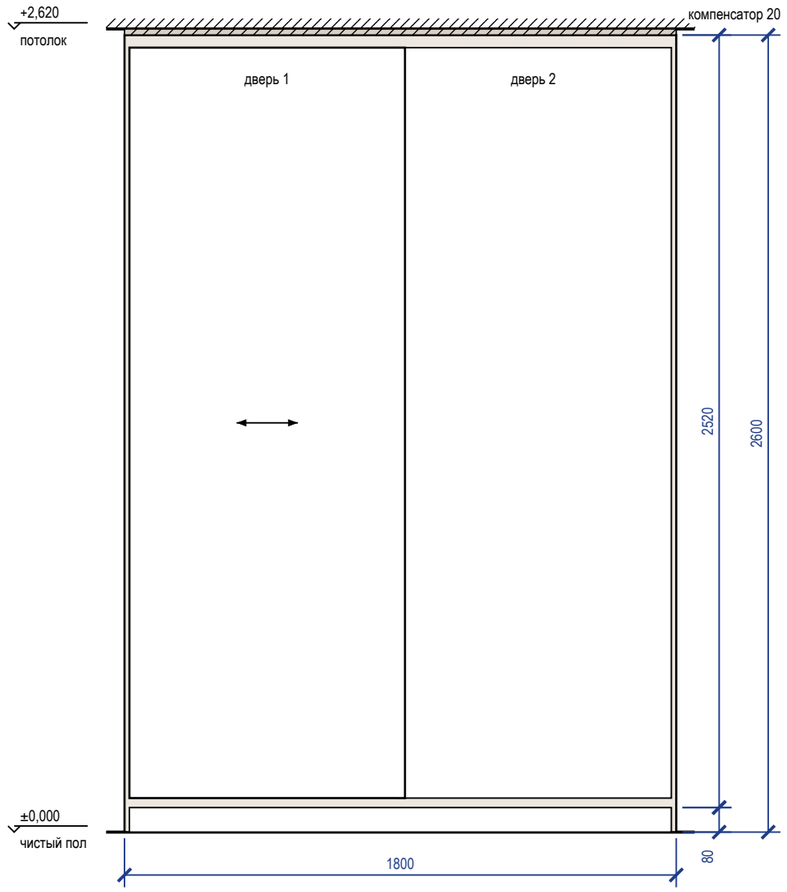


## Вид без фасадов

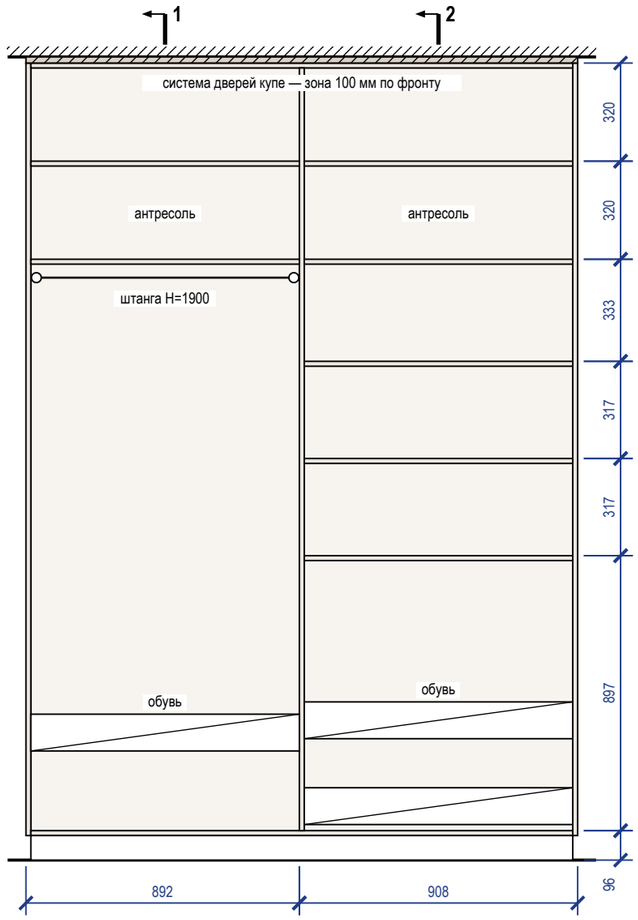


## Разрез 1-1

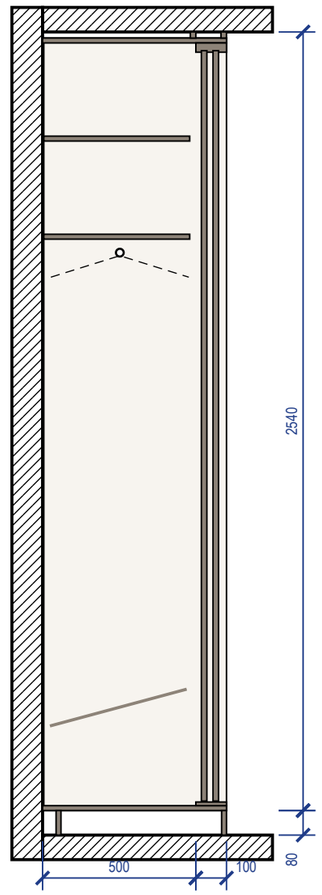


## Разрез 2-2

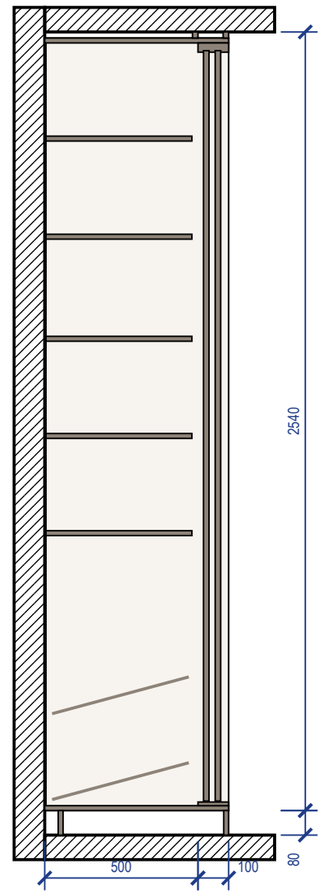


### Примечания

1. Размеры — в мм по чистовой отделке; изделие 1800×600×2600 (Ш×Г×В). Перед раскроем — контрольный замер цеха после чистовой отделки стен, пола и потолка.
2. Корпус — ЛДСП 16 мм, задняя стенка ХДФ 4 мм в паз, цоколь 80 мм на регулируемых опорах; двери купе — ЛДСП 10 мм в алюминиевом профиле, нахлёст 30 мм, ширина двери 899 мм, высота — проём минус 40 мм; цвет — по колерной карте.
3. Кромка: скрытые торцы 0,4 мм, видимые 2 мм (ПВХ/АБС).
4. Номинальные зазоры: дверь купе — боковина 3 мм, фасад ящика — стойка 2 мм; ящики внутри купе — с накладкой 30 мм на стойке со стороны нахлёста дверей.
5. Ящики — направляющие полного выдвижения NL 450 (внутренняя глубина 496 мм ≥ NL + 3); присадка по 32-й системе — выполняет цех.
6. Компенсатор 20 мм — короб из ЛДСП по фронту и торцам, подгоняется к потолку при монтаже (припуск 20 мм), крепится к корпусу и к потолку.
7. Сборка стоя на месте (решение по изделию): корпус не собирается лёжа и не поднимается собранным — собирается в проектном положении у стены; траектория подъёма на виде не показана. Диагональ боковины $\sqrt{(2600^2 + 600^2)} = 2668$ мм > 2620 мм до потолка: поднять собранный корпус нельзя.
8. Крепление к стене от опрокидывания — уголки 2 шт. к несущему основанию (монтажная схема шкафов).

## 3D орто

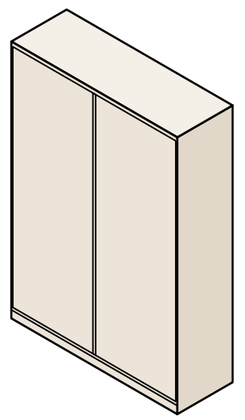

| | | | | | |
|---|---|---|---|---|---|
| | | | | | Проект: Трёхкомнатная квартира |
| | Лист | № док. | Подпись | Дата | |
| Дизайнер | Кырлан А.С. | | | 05.10.26 | Шкаф-купе М_13 |

| Стадия | Лист | Листов |
|---|---|---|
| П | Д_3 | 89 |

выпуск 05.10.2026 № 6a37468da7 · стр. 85 из 89

## Вид с фасадами

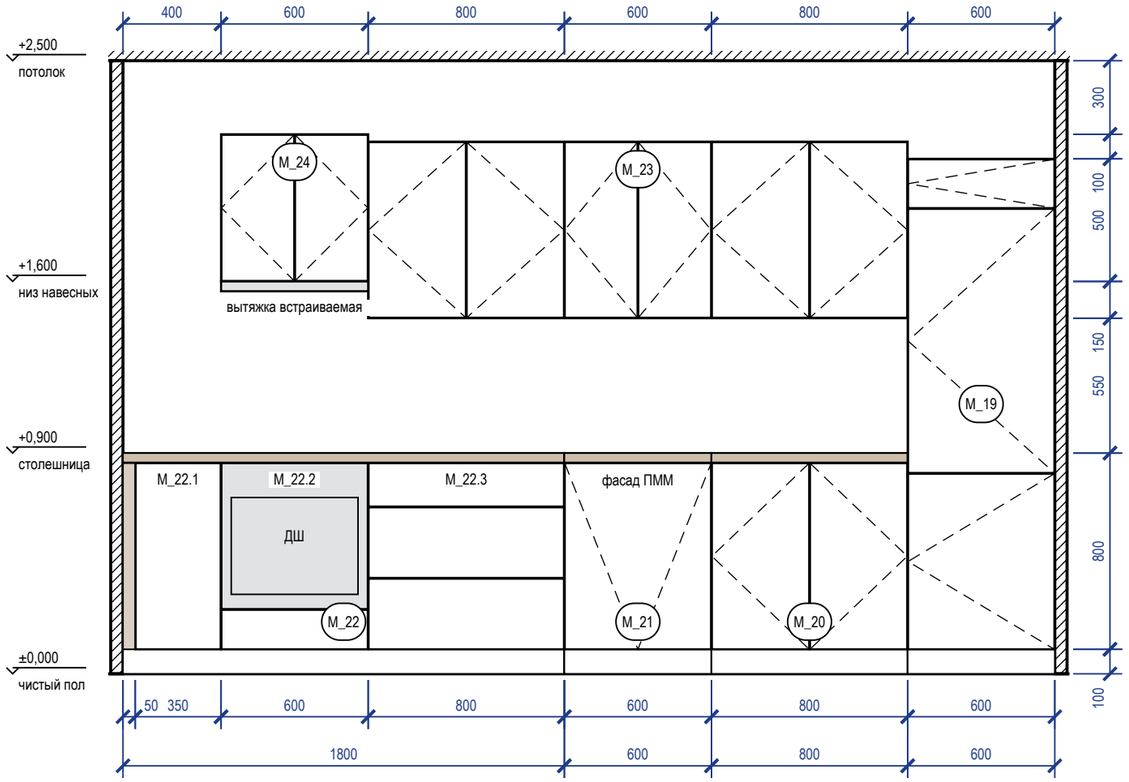


## Вид без фасадов (наполнение, выводы)

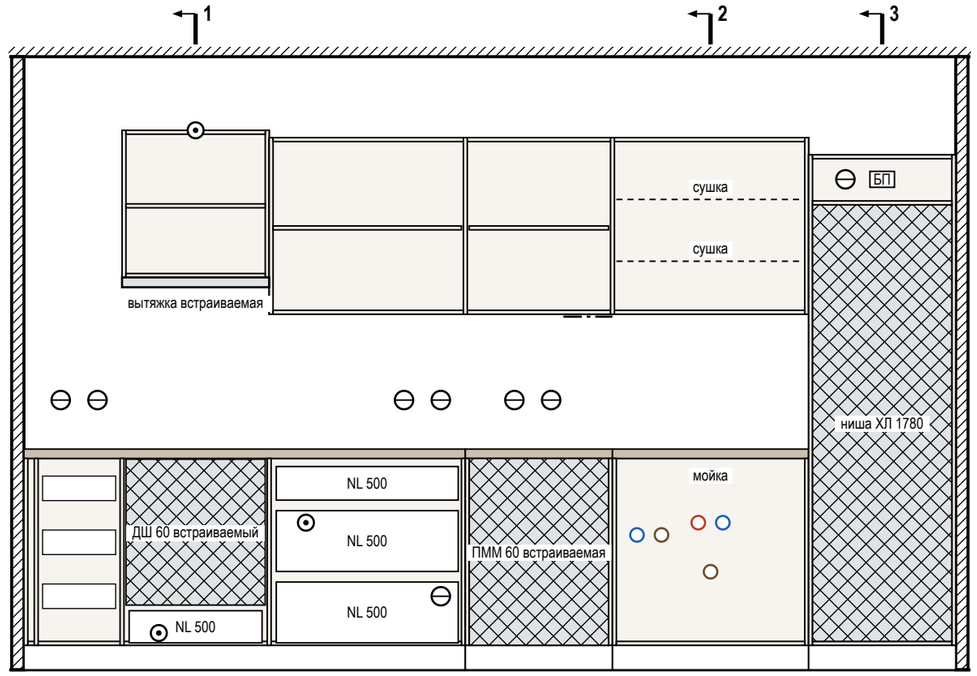


## Разрез 1-1

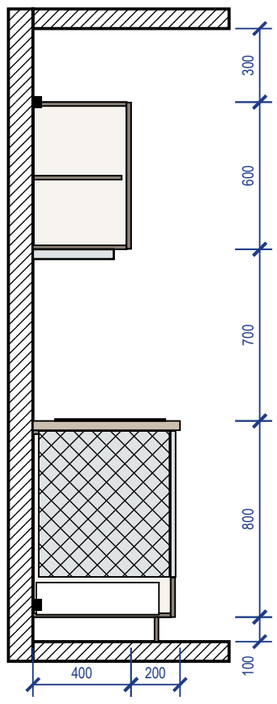


## Разрез 2-2

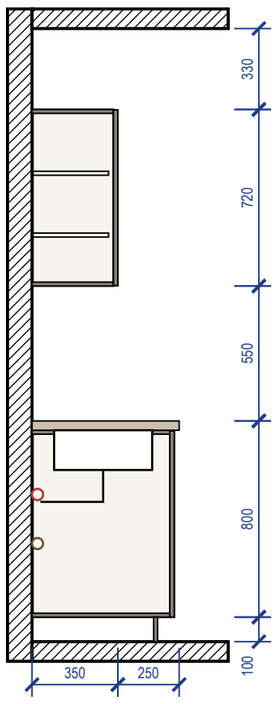


## Разрез 3-3

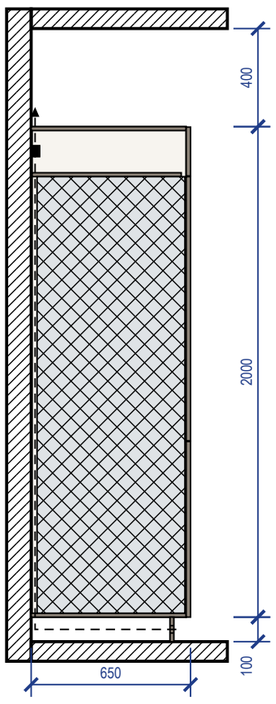


## 3D орто

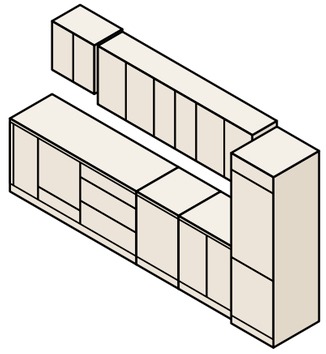

## Примечания

1. Размеры — в мм по чистовой отделке, вид из помещения; марки — как на плане расстановки. Перед раскроем — контрольный замер цеха после фартука и пола.
2. Корпуса — ЛДСП 16 мм, задняя стенка ХДФ 4 мм; фасады — МДФ, эмаль матовая 18 мм, цвет по колерной карте; столешница 38 мм, свес 20 мм; цоколь 100 мм.
3. Кромка: скрытые торцы 0,4 мм, видимые 2 мм. Номинальные зазоры: между фасадами 3 мм, фасад — столешница 3 мм, фасад — стена не менее 3 мм.
4. Ящики полного выдвижения и петли — с доводчиком; присадка по 32-й системе — выполняет цех.
5. Вытяжка встраивается в навесной модуль над варочной: её низ 660 мм над панелью.
6. Ниши техники (холодильник — ориентир 1780 мм) — по монтажным схемам выбранных моделей: решётка в цоколе и канал за пеналом холодильника, зазор за духовым шкафом, фасад ПММ на двери машины.

| | | | | | | |
|---|---|---|---|---|---|---|
| | | | | | Проект: Трёхкомнатная квартира | |
| | Лист | № док. | Подпись | Дата | | |
| Дизайнер | Кырлан А.С. | | | 05.10.26 | Кухня (пом. 6). Развёртка гарнитура | Стадия: П; Лист: Д_4; Листов: 89 |

выпуск 05.10.2026 № 6a37468da7 · стр. 86 из 89

## Ведомость отделки помещений (форма 1 прил. А ГОСТ 21.501-2018)

| № | Наименование помещения | Потолок | | | Стены и перегородки | | | Низ стен (плинтус) | | | Пол | | Примечание |
|---|---|---|---|---|---|---|---|---|---|---|---|---|---|
| | | Вид отделки | Код цвета | S, м² | Вид отделки | Код цвета | S, м² | Вид отделки | Код цвета | L, м | Вид отделки | S, м² | |
| 1 | Спальня 1<br>17,75 м² | ГКЛ по каркасу П113, отм. +2,500; +2,600; окраска, Tikkurila Anti-Reflex 2, глубокоматовая, 2 слоя, подготовка Q3 | Tikkurila V503 | 17,75 | Окраска, Farrow & Ball Modern Emulsion, матовая, 2 слоя, подготовка Q3<br><br>Акцент — стена А: окраска, Farrow & Ball Modern Emulsion, матовая, 2 слоя, подготовка Q3 | Farrow & Ball No. 241<br><br>Farrow & Ball No. 30 | 25,00<br><br>14,18 | Плинтус МДФ h=80 мм, аналог: МДФ под покраску 80×16 | Farrow & Ball No. 241 | 16,8 | Аналог: инженерная доска, дуб натуральный, масло, 1-полосная, 14/4 мм, на клею; тип 1, отм. ЧП ±0,000 | 17,75 | Н стен 2500 (до потолка); плинтус в цвет: стены |
| 2 | Ванная<br>4,43 м² | ГКЛВ по каркасу П113, отм. +2,389; окраска, Tikkurila Luja 7, матовая, 2 слоя, подготовка Q3 | Tikkurila V503 | 4,43 | Облицовка плиткой, аналог: керамогранит под травертин, матовый, 600×1200×9 мм, клей C2 TE S1, затирка CG2WA | по артикулу | 18,61 | нет | | | Аналог: керамогранит ректифицированный под травертин, матовый, 600×600×9 мм; тип 2, отм. ЧП −0,015 | 4,43 | Н стен 2404 (до потолка); гидроизоляция обмазочная, 2 слоя, с заведением на стены 200 мм (по пирогу пола); тест проливом и акт скрытых работ |
| 3 | Гардеробная<br>1,85 м² | Окраска, Tikkurila Anti-Reflex 2, глубокоматовая, 2 слоя, подготовка Q3 | Tikkurila V503 | 1,85 | Окраска, Tikkurila Harmony, матовая, 2 слоя, подготовка Q3 | Tikkurila V503 | 14,74 | Плинтус МДФ h=80 мм, аналог: МДФ под покраску 80×16 | Tikkurila V503 | 5,3 | Аналог: инженерная доска, дуб натуральный, масло, 1-полосная, 14/4 мм, на клею; тип 1, отм. ЧП ±0,000 | 1,85 | Н стен 2700 (до потолка); плинтус в цвет: стены |
| 4 | Спальня 2<br>12,80 м² | ГКЛ по каркасу П113, отм. +2,500; +2,600; окраска, Tikkurila Anti-Reflex 2, глубокоматовая, 2 слоя, подготовка Q3 | Tikkurila V503 | 12,80 | Окраска, Farrow & Ball Modern Emulsion, матовая, 2 слоя, подготовка Q3<br><br>Акцент — стена А: окраска, Farrow & Ball Modern Emulsion, матовая, 2 слоя, подготовка Q3 | Farrow & Ball No. 241<br><br>Farrow & Ball No. 30 | 22,21<br><br>10,22 | Плинтус МДФ h=80 мм, аналог: МДФ под покраску 80×16 | Farrow & Ball No. 241 | 13,6 | Аналог: инженерная доска, дуб натуральный, масло, 1-полосная, 14/4 мм, на клею; тип 1, отм. ЧП ±0,000 | 12,80 | Н стен 2500 (до потолка); плинтус в цвет: стены |
| 5 | Прихожая<br>7,13 м² | ГКЛ по каркасу П113, отм. +2,620; окраска, Tikkurila Anti-Reflex 2, глубокоматовая, 2 слоя, подготовка Q3 | Tikkurila V503 | 7,13 | Окраска, Farrow & Ball Modern Emulsion, матовая, 2 слоя, подготовка Q3 | Farrow & Ball No. 241 | 21,86 | Плинтус МДФ h=80 мм, аналог: МДФ под покраску 80×16 | Farrow & Ball No. 241 | 7,8 | Аналог: керамогранит ректифицированный под травертин, матовый, 600×1200×9 мм; тип 3, отм. ЧП ±0,000 | 7,13 | Н стен 2620 (до потолка); матовая моющаяся, класс 1 EN 13300 — осознанно вместо полуматовой; плинтус в цвет: стены |
| 6 | Кухня-гостиная<br>29,20 м² | ГКЛ по каркасу П113, отм. +2,500; +2,600; окраска, Tikkurila Anti-Reflex 2, глубокоматовая, 2 слоя, подготовка Q3 | Tikkurila V503 | 29,20 | Окраска, Farrow & Ball Modern Emulsion, матовая, 2 слоя, подготовка Q3<br><br>Акцент — стена А: окраска, Farrow & Ball Modern Emulsion, матовая, 2 слоя, подготовка Q3<br>Фартук кухни (стена В): облицовка керамогранитом, аналог: керамогранит под травертин, матовый, 1200×600×9 мм, клей C2 TE S1, затирка CG2WA | Farrow & Ball No. 241<br><br>Farrow & Ball No. 30<br><br>по артикулу | 35,51<br><br>14,18<br><br>1,87 | Плинтус МДФ h=80 мм, аналог: МДФ под покраску 80×16 | Farrow & Ball No. 241 | 22,2 | Аналог: инженерная доска, дуб натуральный, масло, 1-полосная, 14/4 мм, на клею; тип 1, отм. ЧП ±0,000 | 29,20 | Н стен 2500 (до потолка); матовая моющаяся, класс 1 EN 13300 — осознанно вместо полуматовой; плинтус в цвет: стены |
| 7 | Санузел 2<br>2,29 м² | ГКЛВ по каркасу П113, отм. +2,389; окраска, Tikkurila Luja 7, матовая, 2 слоя, подготовка Q3 | Tikkurila V503 | 2,29 | Облицовка плиткой, аналог: керамогранит под травертин, матовый, 600×1200×9 мм, клей C2 TE S1, затирка CG2WA | по артикулу | 13,10 | нет | | | Аналог: керамогранит ректифицированный под травертин, матовый, 600×600×9 мм; тип 2, отм. ЧП −0,015 | 2,29 | Н стен 2404 (до потолка); гидроизоляция обмазочная, 2 слоя, с заведением на стены 200 мм (по пирогу пола); тест проливом и акт скрытых работ |
| 8 | Коридор<br>3,50 м² | ГКЛ по каркасу П113, отм. +2,620; окраска, Tikkurila Anti-Reflex 2, глубокоматовая, 2 слоя, подготовка Q3 | Tikkurila V503 | 3,50 | Окраска, Farrow & Ball Modern Emulsion, матовая, 2 слоя, подготовка Q3 | Farrow & Ball No. 241 | 14,17 | Плинтус МДФ h=80 мм, аналог: МДФ под покраску 80×16 | Farrow & Ball No. 241 | 4,5 | Аналог: инженерная доска, дуб натуральный, масло, 1-полосная, 14/4 мм, на клею; тип 1, отм. ЧП ±0,000 | 3,50 | Н стен 2620 (до потолка); матовая моющаяся, класс 1 EN 13300 — осознанно вместо полуматовой; плинтус в цвет: стены |
| | **Итого** | | | **78,95** | | | **205,64** | | | **70,3** | | **78,95** | |

### Примечания

1. Площади поверхностей — по чистым граням стен до отделки: стены = периметр × высоту от чистого пола помещения до низа потолка минус проёмы (облицовка плиткой — до верха облицовки); плинтус = периметр минус дверные проёмы; пол и потолок — по площади помещения. Количество плиток по раскладке. Площади помещений — с учётом всех частей помещения; откосы в площадь стен не входят.
2. Акцентные стены и фартук — отдельными строками, их площадь вычтена из основной отделки стен помещения; фартук — над нижними модулями кухни от столешницы до низа навесных шкафов, где шкафов нет — на 600 мм.
3. Плинтус — длина по периметру за вычетом дверных проёмов; примыкания к наличникам и встроенной мебели — по развёрткам.
4. Формат плитки — Ш×В×Т (ширина × высота в положении укладки × толщина), мм; на полу — вдоль стен А/В × вдоль стен Б/Г.
5. Коды цвета — по веерам производителей; колеровка каждой краски одной партией, проверка выкраса при свете D65 и при лампах проекта.
6. Уровни подготовки Q1–Q4 — система Knauf, не норма ГОСТ/СП; допуски поверхностей — по СП 71.13330.2017 (действующая редакция).
7. «аналог:» — изделие задано характеристиками, марку и артикул согласовать с заказчиком до закупки.
8. Сводка площадей по материалам, м²: потолок — Tikkurila V503 Anti-Reflex 2 — 72,23; потолок — Tikkurila V503 Luja 7 — 6,72; стены — Farrow & Ball No. 241 Modern Emulsion — 118,75; стены — Farrow & Ball No. 30 Modern Emulsion — 38,58; стены — облицовка плиткой 600×1200×9 мм — 31,71; стены — Tikkurila V503 Harmony — 14,74; фартук — облицовка керамогранитом 1200×600×9 мм — 1,87.

| | | | | | |
|---|---|---|---|---|---|
| | | | | | Проект: Трёхкомнатная квартира |
| | Лист | № док. | Подпись | Дата | |
| Дизайнер | Кырлан А.С. | | | 05.10.26 | Ведомость отделки помещений |

| Стадия | Лист | Листов |
|---|---|---|
| П | С1 | 89 |

выпуск 05.10.2026 № 6a37468da7 · стр. 87 из 89

| Поз. | Наименование и техническая характеристика | Тип, марка, обозначение документа | Код продукции | Поставщик | Ед. изм. | Кол. | Образец | Примечание |
|---|---|---|---|---|---|---|---|---|
| | **Лакокрасочные материалы** | | | | | | | |
| 1 | Краска интерьерная водно-дисперсионная акриловая для стен, матовая, класс мокрого истирания 1 по EN 13300, база A; цвет Farrow & Ball No. 241 «Skimming Stone», колеровка машинная | Farrow & Ball Modern Emulsion | | Farrow & Ball | л | 32,5 | | поз. К1 колерной карты; пом. 1, 4, 5, 6, 8; S = 118,8 м² × 2 сл. × 0,12 л/м² = 28,5 л, +10 % и 0,5 л на подкраску → ≥ 31,9 л; тара 6 × 5 л + 1 × 2,5 л |
| 2 | Краска интерьерная водно-дисперсионная акриловая для акцентных стен, матовая, класс мокрого истирания 1 по EN 13300, база C; цвет Farrow & Ball No. 30 «Hague Blue», колеровка машинная | Farrow & Ball Modern Emulsion | | Farrow & Ball | л | 12,5 | | поз. К2 колерной карты; пом. 1, 4, 6; S = 38,6 м² × 2 сл. × 0,12 л/м² = 9,3 л, +10 % и 0,5 л на подкраску → ≥ 10,7 л; тара 2 × 5 л + 1 × 2,5 л |
| 3 | Краска интерьерная водно-дисперсионная акриловая для потолков, глубокоматовая, класс мокрого истирания 2 по EN 13300, база A; цвет Tikkurila V503 «Winter», колеровка машинная | Tikkurila Anti-Reflex 2 | | Tikkurila | л | 19,8 | | поз. К3 колерной карты; пом. 1, 3, 4, 5, 6, 8; S = 72,2 м² × 2 сл. × 0,12 л/м² = 17,3 л, +10 % и 0,5 л на подкраску → ≥ 19,6 л; тара 2 × 9 л + 2 × 0,9 л |
| 4 | Краска интерьерная водно-дисперсионная акриловая для потолков, матовая, класс мокрого истирания 1 по EN 13300, база A; цвет Tikkurila V503 «Winter», колеровка машинная | Tikkurila Luja 7 | | Tikkurila | л | 2,7 | | поз. К5 колерной карты; пом. 2, 7; S = 6,7 м² × 2 сл. × 0,12 л/м² = 1,6 л, +10 % и 0,5 л на подкраску → ≥ 2,3 л; тара 1 × 2,7 л |
| 5 | Краска интерьерная водно-дисперсионная акриловая для стен, матовая, класс мокрого истирания 1 по EN 13300, база A; цвет Tikkurila V503 «Winter», колеровка машинная | Tikkurila Harmony | | Tikkurila | л | 4,5 | | поз. К6 колерной карты; пом. 3; S = 14,7 м² × 2 сл. × 0,12 л/м² = 3,5 л, +10 % и 0,5 л на подкраску → ≥ 4,4 л; тара 1 × 2,7 л + 2 × 0,9 л |
| 6 | Краска для МДФ и дерева в цвет Farrow & Ball No. 241 «Skimming Stone» — окраска плинтуса; блеск не ниже блеска стен | марка не задана | | | л | 1,7 | | поз. К4; пом. 1, 4, 5, 6, 8; L = 65,1 м, S = 6,2 м² × 2 сл. × 0,12 л/м² + 10 %; продукт подобрать в веере Farrow & Ball |
| 7 | Краска для МДФ и дерева в цвет Tikkurila V503 «Winter» — окраска плинтуса; блеск не ниже блеска стен | марка не задана | | | л | 0,5 | | поз. К7; пом. 3; L = 5,3 м, S = 0,5 м² × 2 сл. × 0,12 л/м² + 10 %; продукт подобрать в веере Tikkurila |
| 8 | Грунтовка акриловая под окраску стен и потолков — из системы производителя краски | по системе краски | | | м² | 252 | | площадь окраски стен, акцентов и потолков; 1 слой перед окраской; расход — по ТУ грунтовки |
| | **Плитка и керамогранит** | | | | | | | |
| 9 | Керамогранит под травертин, 600×600×9 мм, ректификат, водопоглощение 0,1 % (BIa), противоскольжение R10, PEI IV | аналог по характеристикам | | | м² | 9,72 | | шов 2 мм; Ванная, пол; Санузел 2, пол; по раскладке 24 шт (S = 6,72 м²), с запасом 27 шт |
| 10 | Керамогранит под травертин, 600×1200×9 мм, ректификат, водопоглощение 0,1 % | аналог по характеристикам | | | м² | 54 | | шов 2 мм; Ванная, стены А–Г; Ванная, короб инсталляции; Санузел 2, стены А–Г; Санузел 2, короб инсталляции; по раскладке 65 шт (S = 33,26 м²), с запасом 75 шт |
| 11 | Керамогранит ректифицированный под травертин, матовый, 600×1200×9 мм, водопоглощение 0,1 % (BIa), противоскольжение R10, PEI IV | аналог по характеристикам | | | м² | 10,08 | | шов 2 мм; Прихожая, пол; по раскладке 12 шт (S = 7,13 м²), с запасом 14 шт |
| 12 | Керамогранит под травертин, матовый, 1200×600×9 мм, ректификат, водопоглощение 0,1 % (BIa) | аналог по характеристикам | | | м² | 3,60 | | шов 2 мм; Кухня-гостиная, фартук (ст. В); по раскладке 4 шт (S = 1,87 м²), с запасом 5 шт |
| | **Напольные покрытия** | | | | | | | |
| 13 | Инженерная доска, дуб натуральный, масло, 1-полосная, 14/4 мм, эмиссия E1, укладка на клей | аналог по характеристикам | | | м² | 69,7 | | пом. 1, 3, 4, 6, 8; S = 65,10 м² + 7 % (прямая укладка); к заказу — кратно упаковке |
| 14 | Клей для паркета и инженерной доски, эластичный (СМП / полиуретановый) | по рекомендации производителя доски | | | м² | 66 | | площадь приклейки; расход и шпатель — по ТУ клея |
| | **Погонажные изделия** | | | | | | | |
| 15 | Плинтус МДФ под покраску 80×16, крепление к стене, окраска в цвет Farrow & Ball No. 241 | аналог по характеристикам | | | м | 78 | | пом. 1, 3, 4, 5, 6, 8; L = 70,3 м (периметр без дверных проёмов) + 10 % на подрезку; в штуках — по длине планки |
| | **Смеси и материалы для облицовки** | | | | | | | |
| 16 | Затирка для швов плитки, класс CG2WA по EN 13888 | Mapei Ultracolor Plus 132 | | Mapei | кг | 3,8 | | по раскладке (a+b)/(a·b) × шов × t × 1,6 + 10 %; в т. ч. 0,7 кг — позиции раскладки без марки |
| 17 | Клей плиточный C2 TE S1 по EN 12004, слой 5 мм | Ceresit CM 17 | | Ceresit | кг | 385 | | 16 меш. по 25 кг; 1,5 кг/м² на 1 мм слоя + 10 %; в т. ч. 73 кг — позиции раскладки без марки |
| 18 | Гидроизоляция обмазочная мокрых зон: пол, стены по периметру, зоны замачивания; 2 слоя с армирующей лентой в углах | аналог по характеристикам | | | м² | 20 | | площадь по листу раскладки плитки + 10 %; расход смеси — по ТУ |
| 19 | Лента демпферная по периметру пола из плитки | аналог по характеристикам | | | м | 22,4 | | периметр без дверных проёмов + 10 % |

## Примечания

1. Количества — из геометрии проекта: площади поверхностей по чистым граням стен до отделки (те же, что в ведомости отделки и колерной карте), плитка, клей и затирка — по раскладке плиточника; в графе «Кол.» — к заказу, с запасом.
2. Краска: расход 0,12 л/м² на слой в 2 слоя, если по ТУ не задан иной; запас 10 % и 0,5 л на подкраску каждого кода. Один код — одна партия, колеровка машинная в колеровочном центре бренда; в заказ — только после утверждения выкраса (колерная карта). Фасовка — по каталогу бренда на дату выпуска; к заказу — не меньше расчётного объёма.
3. «Аналог по характеристикам» — допускается изделие другого производителя с характеристиками не ниже указанных, по согласованию с автором проекта.
4. Графы «Код продукции» и «Масса 1 ед.» не заполнены: коды по классификатору продукции не присвоены, масса единицы до 25 кг (ГОСТ 21.110-2013).
5. Грунтовка и клей для доски указаны площадью обработки; объём — по ТУ выбранного продукта.

| | | | | | |
|---|---|---|---|---|---|
| | | | | | Проект: Трёхкомнатная квартира |
| | Лист | № док. | Подпись | Дата | |
| Дизайнер | Кырлан А.С. | | | 05.10.26 | Спецификация отделочных материалов |

| Стадия | Лист | Листов |
|---|---|---|
| П | С2 | 89 |

### 1 Порог 15 мм: мокрая зона — жилое помещение (М 1:10)

Применение: двери Д-5, Д-3

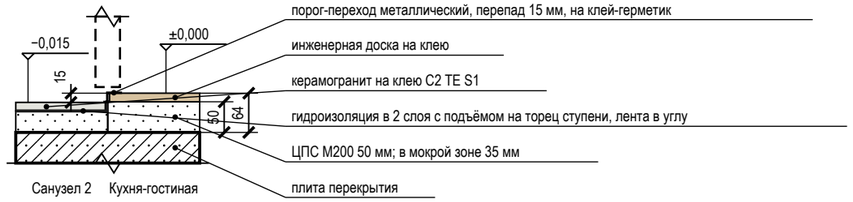


### 2 Стык покрытий пола Т-профилем без перепада (М 1:5)

Применение: проёмы 5↔6, 8↔5

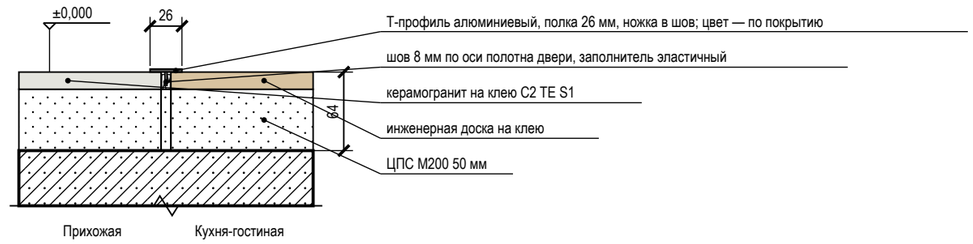


### 3 Дверь скрытого монтажа в плоскости стены, плинтус (М 1:5)

Применение: двери Д-2, Д-5, Д-3, Д-4

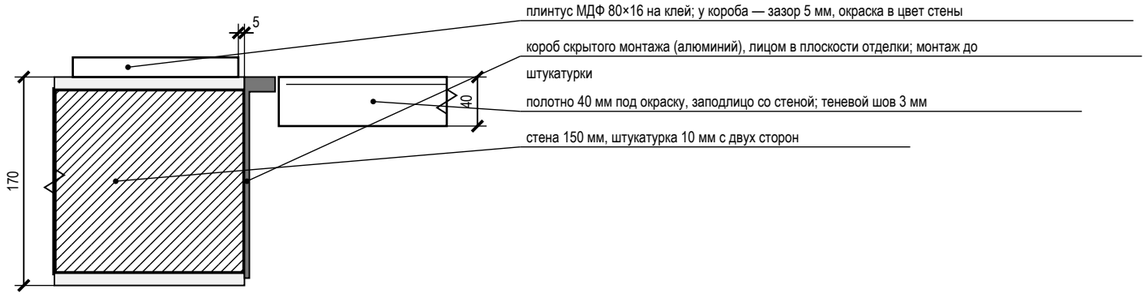


### 4 Короб стояков К1-1, В1-1 с люком и звукоизоляцией (М 1:20)

Применение: пом. 2

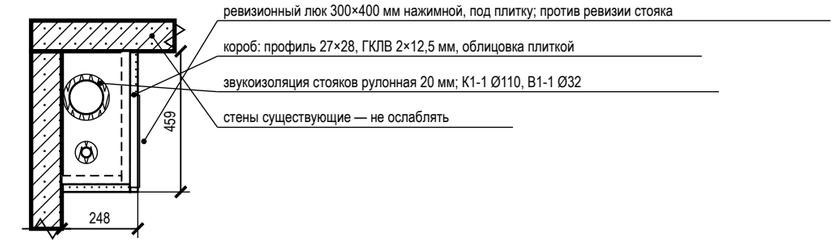


### 5 Гидроизоляция санузла: заход на стены 200 мм, примыкание ванны (М 1:20)

Применение: пом. 2, 7

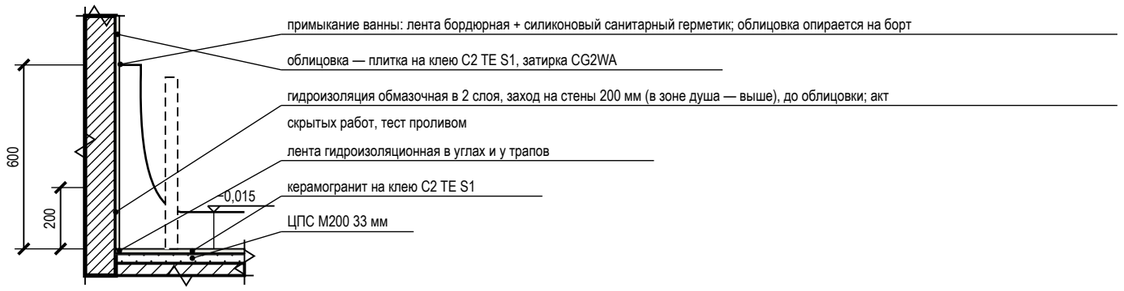


### 6 Плинтус МДФ 80×16 мм у окрашенной стены (М 1:10)

Применение: пом. 1, 3, 4, 5, 6, 8

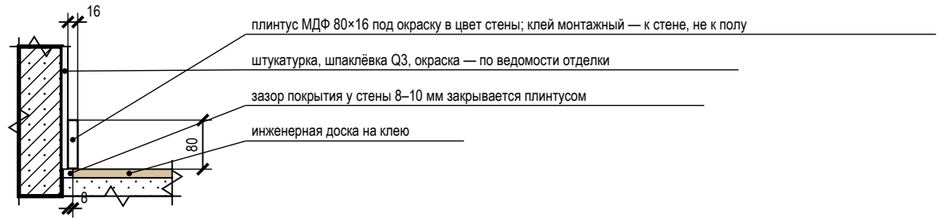


## Условные обозначения

- железобетон (плита, стены)
- кладка, перегородка
- стяжка, раствор
- гипсокартон ГКЛВ
- звукоизоляция, эластичный заполнитель
- плитка, керамогранит на клею
- инженерная доска (покрытие пола)
- металлический профиль (порог, Т-профиль, короб двери)
- гидроизоляция (обмазочная, лента)

## Примечания

1. Узлы — типовые решения проекта для мест, отмеченных выносками на листе схемы расположения развёрток и узлов; размеры — в мм, отметки — в м от ±0,000.
2. Узлы с гидроизоляцией, закладными и коробами скрытого монтажа принимаются по актам скрытых работ до закрытия отделкой; гидроизоляция — после теста проливом (24 ч).
3. Марки изделий (порог, Т-профиль, короб скрытой двери, люк) — по спецификациям; замена — на аналог с теми же габаритами по согласованию с автором проекта.

| | | | | | |
|---|---|---|---|---|---|
| | | | | | Проект: Трёхкомнатная квартира |
| | Лист | № док. | Подпись | Дата | |
| Дизайнер | Кырлан А.С. | | | 05.10.26 | Узлы |

| Стадия | Лист | Листов |
|---|---|---|
| П | С3 | 89 |

выпуск 05.10.2026 № 6a37468da7 · стр. 89 из 89