LINEA

РАБОЧАЯ ДОКУМЕНТАЦИЯ

# Квартира с кабинетом

*современный модерн*

Шифр комплекта ГД-2026-008-АИ

Стадия РП

Дата выпуска 18.10.2026

ПРЕДВАРИТЕЛЬНО · не для производства работ
открыто пунктов: 4 (реестр — л. 6)

ДИЗАЙНЕР

Кырлан Александр Сергеевич

выпуск 18.10.2026 · d2d5a25dca · стр. 1 из 129

# Содержание

ПРЕДВАРИТЕЛЬНО · не для производства работ · открыто пунктов: 4 (реестр — л. 6)

03 Общие данные 11 л.

14 Архитектурные решения 3 л.

18 Планировочное решение 5 л.

24 Электрооборудование 8 л.

33 Отопление и вентиляция 2 л.

36 Водоснабжение и канализация 4 л.

41 Потолки и ГКЛ-конструкции 5 л.

47 Полы и отделка 7 л.

55 Декор и текстиль 15 л.

71 Развёртки и узлы 25 л.

97 Смета 7 л.

105 Визуализации 24 л.

ДИЗАЙН-ПРОЕКТ ИНТЕРЬЕРА

# Квартира с кабинетом

## *современный модерн*

**127,29 м²**

природность · плавность · камерность · ремесленность · поэтичность · приглушённая цветность · сумеречный тёплый свет

Современный модерн 2026: модерн 60 % + современный (contemporary.json) 40 %. Стены — Bone No. 15 и льняной беж S 2010-Y30R, потолки — Winter V503, шалфей Calke Green No. 34 и пудровый Peignoir No. 286 вторым планом, акценты павлиний S 5030-B10G (бархат), горчица India Yellow No. 66, морёный дуб S 8010-Y30R; металл — латунь.

ПАЛИТРА 60 / 30 / 10

| F&B No. 15 | NCS S 2010-Y30R | V503 | F&B No. 34 | F&B No. 286 |
|---|---|---|---|---|
| 60 % | 60 % | 60 % | 30 % | 30 % |

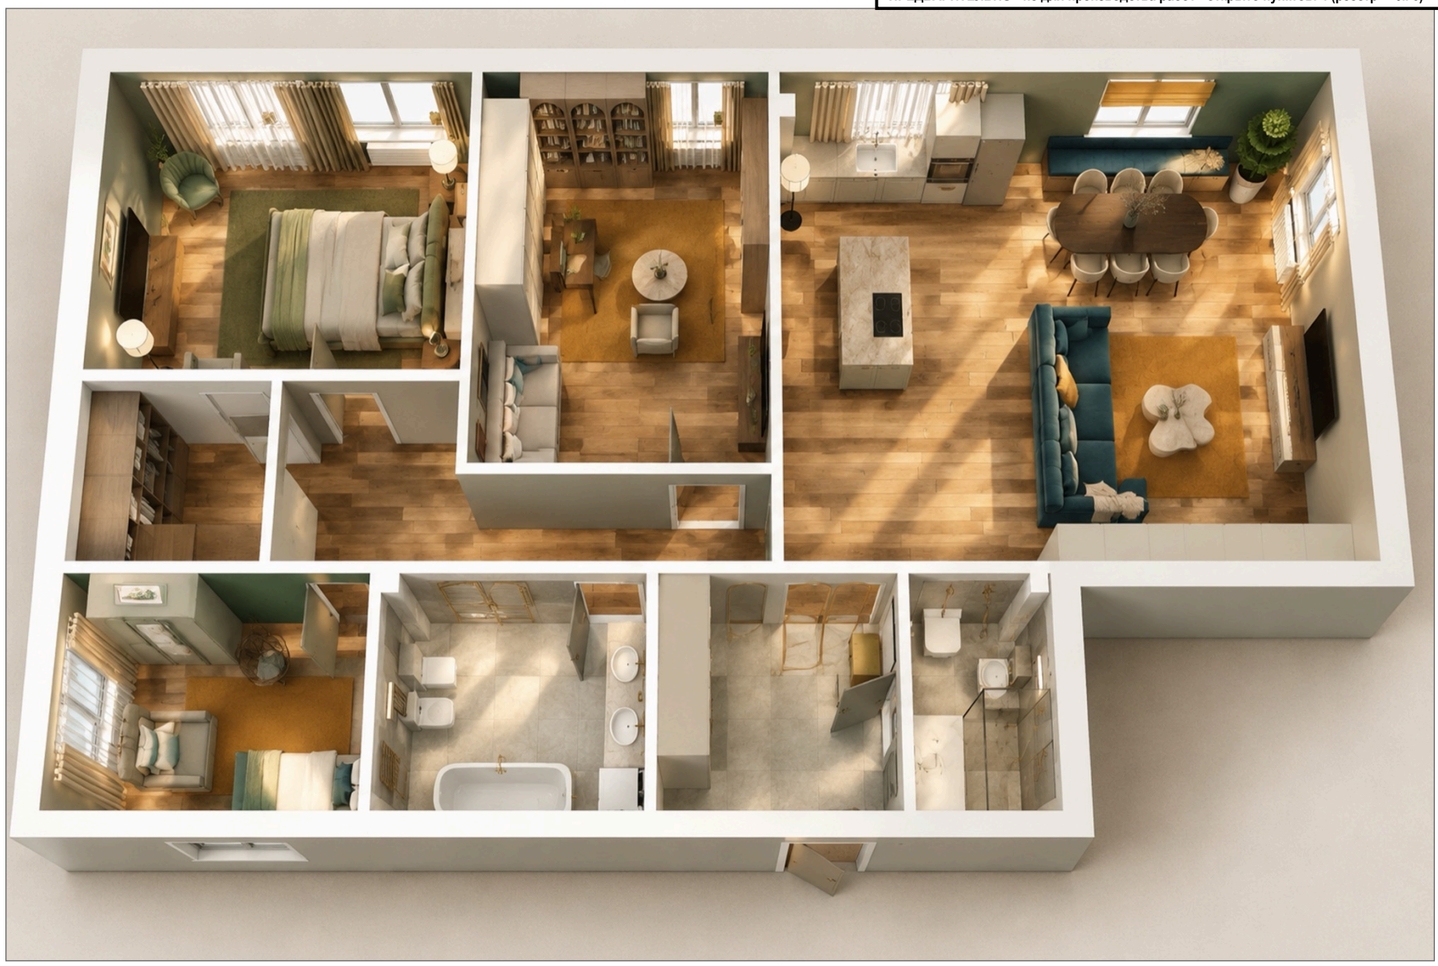

Визуализация 1 · Вид сверху (3D): планировка с мебелью, текстилем и декором

| ОБЪЕКТ | ОБЩАЯ ПЛОЩАДЬ | ПОМЕЩЕНИЙ |
|---|---|---|
| Квартира с кабинетом | 127,29 м² | 9, из них жилых 4 |

| СТИЛЬ | СТАДИЯ | ШИФР |
|---|---|---|
| Модерн (ар-нуво) · современный модерн | Рабочий проект · предварительно | ГД-2026-008-АИ |

АВТОР ПРОЕКТА

Кырлан Александр Сергеевич

Октябрь 2026

| Изм. | Кол.уч | Лист | № док. | Подп. | Дата |
|---|---|---|---|---|---|
| Разраб. | | Кырлан А.С. | | | 18.10.26 |
| Пров. | | | | | |
| ГИП | | | | | |
| | | | | | |
| Н. контр. | | | | | |
| Утв. | | | | | |

**ГД-2026-008-АИ**

Квартира с кабинетом

Общая площадь 127,29* м² · * размеры со скана, не замерены (реестр — л. 6, К-1)

| Дизайн-проект интерьера | Стадия | Лист | Листов |
|---|---|---|---|
| | РП | 1 | 92 |

**Титульный лист**

М б/м

**Кырлан Александр Сергеевич**

выпуск 18.10.2026 № d2d5a25dca · стр. 3 из 129

# Общие данные

Комплект ГД-2026-008-АИ · Квартира с кабинетом · современный модерн

**ПРЕДВАРИТЕЛЬНО · не для производства работ · открыто пунктов: 4 (реестр — л. 6)**

### Ведомость рабочих чертежей основного комплекта ГД-2026-008-АИ

| Лист | Наименование | Примечание |
|---|---|---|
| 1 | Титульный лист | |
| 2 | Общие данные | |
| 3 | Общие данные | |
| 4 | Общие данные | |
| 5 | Общие данные | |
| 6 | Открытые вопросы, принятые допущения и конфликты | |
| 7 | Задание на контрольный обмер и обследование. Лист 1 из 2 | |
| 8 | Задание на контрольный обмер и обследование. Лист 2 из 2 | |
| 9 | График закупок и работ. Лист 1 из 3 | |
| 10 | График закупок и работ. Лист 2 из 3 | |
| 11 | График закупок и работ. Лист 3 из 3 | |
| 12 | Обмерный план | |
| 13 | План демонтажа и монтажа перегородок | |
| 14 | План дверей и ведомость заполнения проёмов | |
| 15 | Концепция интерьера | |
| 16 | План расстановки мебели | |
| 17 | Спецификация мебели и оборудования | |
| 18 | Спецификация мебели и оборудования (продолжение) | |
| 19 | Спецификация мебели и оборудования (продолжение) | |
| 20 | План розеток и электровыводов | |
| 21 | План освещения | |
| 22 | План выключателей и схема включения | |
| 23 | Ведомость электроточек и изделий | |
| 24 | Ведомость электроточек и изделий (продолжение) | |
| 25 | Однолинейная схема щита | |
| 26 | План принципиальных трасс | |
| 27 | План слаботочных сетей | |
| 28 | План вентиляции | |
| 29 | План отопления | |
| 30 | План выводов сантехники Допущения и предложения на листе. См. лист открытых вопросов (лист 6). | |

Общие указания — лист 5: ±0,000 — чистый пол; несущие конструкции и сети дома — по отдельному проекту; скрытые работы — по актам. Открытые вопросы и допущения — лист 6.

### Ведомость рабочих чертежей основного комплекта ГД-2026-008-АИ (продолжение)

| Лист | Наименование | Примечание |
|---|---|---|
| 31 | Схема разводки водопровода и канализации | |
| 32 | Спецификация сантехнического оборудования | |
| 33 | Спецификация светильников и сценарии освещения | |
| 34 | План потолков | |
| 35 | Раскладка плитки. Планы полов | |
| 36 | Раскладка плитки. Прихожая. Фартук кухни | |
| 37 | Раскладка плитки. Ванная. Развёртки стен | |
| 38 | Раскладка плитки. Санузел гостевой. Развёртки стен | |
| 39 | План полов | |
| 40 | Ведомость отделки помещений. Лист 1 из 2 | |
| 41 | Ведомость отделки помещений. Лист 2 из 2 | |
| 42 | Колерная карта | |
| 43 | Спецификация отделочных материалов | |
| 44 | Концепция декора и визуализации | |
| 45 | План текстиля и декора | |
| 46 | Шторы и карнизы | |
| 47 | Ведомость текстиля | |
| 48 | Ведомость декора. Схемы развески | |
| 49 | Встроенная мебель. Схема расположения | |
| 50 | Система хранения Г1 | |
| 51 | Система хранения Г2 | |
| 52 | Шкаф распашной К1 | |
| 53 | Шкаф распашной Кх13 | |

| Изм. | Кол.уч | Лист | № док. | Подп. | Дата |
|---|---|---|---|---|---|
| Разраб. | | Кырлан А.С. | | | 18.10.26 |
| Пров. | | | | | |
| ГИП | | | | | |
| | | | | | |
| Н. контр. | | | | | |
| Утв. | | | | | |

**ГД-2026-008-АИ**

Квартира с кабинетом

Общая площадь 127,29* м² · * размеры со скана, не замерены (реестр — л. 6, К-1)

Дизайн-проект интерьера

| Стадия | Лист | Листов |
|---|---|---|
| РП | 2 | 92 |

**Общие данные**

М б/м

**Кырлан Александр Сергеевич**

выпуск 18.10.2026 № d2d5a25dca · стр. 4 из 129

# Общие данные

Комплект ГД-2026-008-АИ · лист 2 общих данных (продолжение)

Допущения и предложения на листе. См. лист открытых вопросов (лист 6).

### Ведомость рабочих чертежей основного комплекта ГД-2026-008-АИ (продолжение)

| Лист | Наименование | Примечание |
|---|---|---|
| 54 | Шкаф распашной Д1 | |
| 55 | Шкаф-купе П8 | |
| 56 | Кухня (пом. 4). Развёртка гарнитура | |
| 57 | Кухня (пом. 4). Монтажная схема | |
| 58 | Шкафы. Монтажная схема. Лист 1 из 2 | |
| 59 | Шкафы. Монтажная схема. Лист 2 из 2 | |
| 60 | Ведомости изделий, техники и фурнитуры | |
| 61 | Реестр марок отделки и позиций альбома | |
| 62 | Схема расположения развёрток и узлов | |
| 63 | Развёртки стен А, Б. Спальня (пом. 1) | |
| 64 | Развёртки стен В, Г. Спальня (пом. 1) | |
| 65 | Развёртки стен А, Б, В. Гардеробная-постирочная (пом. 2) | |
| 66 | Развёртка стены Г. Гардеробная-постирочная (пом. 2) | |
| 67 | Развёртки стен А, Б. Кабинет (пом. 3) | |
| 68 | Развёртки стен В, Г. Кабинет (пом. 3) | |
| 69 | Развёртка стены Г. Кухня-гостиная (пом. 4), кухонный фронт | |
| 70 | Развёртка стены А. Кухня-гостиная (пом. 4), кухонный фронт | |
| 71 | Развёртка стены Б. Кухня-гостиная (пом. 4) | |
| 72 | Развёртка стены В. Кухня-гостиная (пом. 4) | |
| 73 | Развёртки стен А1, А2. Коридор (пом. 5) | |
| 74 | Развёртки стен В, Г. Коридор (пом. 5) | |
| 75 | Развёртки стен А, Б. Детская (пом. 6) | |
| 76 | Развёртки стен В, Г. Детская (пом. 6) | |
| 77 | Развёртка стены А. Ванная (пом. 7) | |
| 78 | Развёртка стены Б. Ванная (пом. 7) | |
| 79 | Развёртка стены В. Ванная (пом. 7) | |
| 80 | Развёртка стены Г. Ванная (пом. 7) | |
| 81 | Развёртки стен. Прихожая (пом. 8) | |
| 82 | Развёртка стены А. Санузел гостевой (пом. 9) | |
| 83 | Развёртки стен Б, В. Санузел гостевой (пом. 9) | |

### Ведомость рабочих чертежей основного комплекта ГД-2026-008-АИ (продолжение)

| Лист | Наименование | Примечание |
|---|---|---|
| 84 | Развёртка стены Г. Санузел гостевой (пом. 9) | |
| 85 | Узлы | |
| 86 | Ведомость объёмов работ | |
| 87 | Ведомость объёмов работ (продолжение) | |
| 88 | Ведомость объёмов работ (окончание) | |
| 89 | Спецификация материалов | |
| 90 | Спецификация материалов (окончание) | |
| 91 | Смета ориентировочная | |
| 92 | Смета ориентировочная (окончание) | |

### Ведомость ссылочных и прилагаемых документов

| Обозначение | Наименование | Примечание |
|---|---|---|
| | Ссылочные документы | |
| ГОСТ 21.201-2011 | СПДС. Условные графические изображения элементов зданий, сооружений и конструкций | |
| ГОСТ 21.205-2016 | СПДС. Условные обозначения элементов санитарно-технических систем | |
| ГОСТ 21.210-2014 | СПДС. Изображения условные графические электрооборудования и проводок на планах | |
| ГОСТ 2.306-68 | ЕСКД. Обозначения графические материалов и правила их нанесения на чертежах | |
| | Прилагаемые документы | |
| ГД-2026-008-АИ.В1 | Визуализация. Вид сверху (3D): планировка с мебелью, текстилем и декором | альбом визуализаций |
| ГД-2026-008-АИ.В2 | Визуализация. Визуализация «room-bath1-wB» | |
| ГД-2026-008-АИ.В3 | Визуализация. Визуализация «room-bath1-wC» | |

Общие указания — лист 5: ±0,000 — чистый пол; несущие конструкции и сети дома — по отдельному проекту; скрытые работы — по актам. Открытые вопросы и допущения — лист 6.

| Изм. | Кол.уч | Лист | № док. | Подп. | Дата | ГД-2026-008-АИ | | |
|---|---|---|---|---|---|---|---|---|
| | | | | | | Квартира с кабинетом | | |
| | | | | | | Общая площадь 127,29* м² · * размеры со скана, не замерены (реестр — л. 6, К-1) | | |
| Разраб. | | Кырлан А.С. | | | 18.10.26 | Дизайн-проект интерьера | Стадия: РП | Лист: 3 / Листов: 92 |
| Пров. | | | | | | | | |
| ГИП | | | | | | | | |
| Н. контр. | | | | | | Общие данные | Кырлан Александр Сергеевич | |
| Утв. | | | | | | М б/м | | |

выпуск 18.10.2026 № d2d5a25dca · стр. 5 из 129

# Общие данные

Комплект ГД-2026-008-АИ · лист 3 общих данных (продолжение)

## Ведомость ссылочных и прилагаемых документов (продолжение)

| Обозначение | Наименование | Примечание |
|---|---|---|
| ГД-2026-008-АИ.В4 | Визуализация. Визуализация «room-bath1-wD» | |
| ГД-2026-008-АИ.В5 | Визуализация. Визуализация «room-bath2-wC» | |
| ГД-2026-008-АИ.В6 | Визуализация. Визуализация «room-bath2-wide» | |
| ГД-2026-008-АИ.В7 | Визуализация. Визуализация «room-bedroom-wA» | |
| ГД-2026-008-АИ.В8 | Визуализация. Визуализация «room-bedroom-wB» | |
| ГД-2026-008-АИ.В9 | Визуализация. Визуализация «room-bedroom-wD» | |
| ГД-2026-008-АИ.В10 | Визуализация. Визуализация «room-corridor-wC» | |
| ГД-2026-008-АИ.В11 | Визуализация. Визуализация «room-hall-wB» | |
| ГД-2026-008-АИ.В12 | Визуализация. Визуализация «room-hall-wC» | |
| ГД-2026-008-АИ.В13 | Визуализация. Визуализация «room-hall-wD» | |
| ГД-2026-008-АИ.В14 | Визуализация. Визуализация «room-kids-wA» | |
| ГД-2026-008-АИ.В15 | Визуализация. Визуализация «room-kids-wB» | |
| ГД-2026-008-АИ.В16 | Визуализация. Визуализация «room-kids-wD» | |
| ГД-2026-008-АИ.В17 | Визуализация. Визуализация «room-living-wA» | |
| ГД-2026-008-АИ.В18 | Визуализация. Визуализация «room-living-wB» | |
| ГД-2026-008-АИ.В19 | Визуализация. Визуализация «room-living-wC» | |
| ГД-2026-008-АИ.В20 | Визуализация. Визуализация «room-living-wD» | |
| ГД-2026-008-АИ.В21 | Визуализация. Визуализация «room-study-wA» | |
| ГД-2026-008-АИ.В22 | Визуализация. Визуализация «room-study-wB» | |
| ГД-2026-008-АИ.В23 | Визуализация. Визуализация «room-study-wD» | |
| ГД-2026-008-АИ.В24 | Визуализация. Визуализация «room-wardrobe-wide» | |

## Состав дизайн-проекта

| Раздел | Состав | Листы |
|---|---|---|
| Обложка | Дизайн-проект интерьера; Квартира с кабинетом; автор проекта — Кырлан Александр Сергеевич | 1 с. |
| Концепция | Стиль Модерн (ар-нуво) 60 % + Современный (контемпорари) 40 %: концепция интерьера, палитра и материалы (колерная карта — лист 42) | л. 15 |
| Визуализации | 24 изобр.: Вид сверху (3D): планировка с мебелью, текстилем и декором; Визуализация «room-bath1-wB»; Визуализация «room-bath1-wC»; Визуализация «room-bath1-wD»; Визуализация «room-bath2-wC»; Визуализация «room-bath2-wide»; Визуализация «room-bedroom-wA»; Визуализация «room-bedroom-wB»; Визуализация «room-bedroom-wD»; Визуализация «room-corridor-wC»; Визуализация «room-hall-wB»; Визуализация «room-hall-wC»; Визуализация «room-hall-wD»; Визуализация «room-kids-wA»; Визуализация «room-kids-wB»; Визуализация «room-kids-wD»; Визуализация «room-living-wA»; Визуализация «room-living-wB»; Визуализация «room-living-wC»; Визуализация «room-living-wD»; Визуализация «room-study-wA»; Визуализация «room-study-wB»; Визуализация «room-study-wD»; Визуализация «room-wardrobe-wide» | В1–В24 |
| Рабочие чертежи | планы, развёртки, узлы (развёртки и узлы — листы 62–65, 67, 68, 73–76, 81, 83, 85) | л. 1–92 |
| Спецификации и ведомости | оборудование, изделия, отделка, электроточки | л. 14, 17–19, 23, 24, 32, 33, 40–43, 47, 48, 86–90 |

**Допущения и предложения на листе**

Основа листа: размеры сняты с растрового плана заказчика с частичными размерами: рисунок не в масштабе, помещения выровнены по подписанным размерам мебели и проходов; контрольный обмер не выполнен (К-1); высота потолка 2700 мм принята: на плане заказчика её нет (К-2); толщины стен 300 / 120 мм приняты по плану заказчика, не замерены (К-1); разрешённая мощность 15 кВт принята по типовым ТУ для квартиры, ТУ заказчиком не переданы (К-4).
См. лист открытых вопросов (лист 6, записи К-1, К-2, К-4).

Общие указания — лист 5: ±0,000 — чистый пол; несущие конструкции и сети дома — по отдельному проекту; скрытые работы — по актам. Открытые вопросы и допущения — лист 6.

| Изм. | Кол.уч | Лист | № док. | Подп. | Дата |
|---|---|---|---|---|---|
| Разраб. | | Кырлан А.С. | | | 18.10.26 |
| Пров. | | | | | |
| ГИП | | | | | |
| Н. контр. | | | | | |
| Утв. | | | | | |

**ГД-2026-008-АИ**

Квартира с кабинетом

Общая площадь 127,29* м² · * размеры со скана, не замерены (реестр — л. 6, К-1)

Дизайн-проект интерьера

| Стадия | Лист | Листов |
|---|---|---|
| РП | 4 | 92 |

**Общие данные**

М б/м

**Кырлан Александр Сергеевич**

выпуск 18.10.2026 № d2d5a25dca · стр. 6 из 129

# Общие данные

Комплект ГД-2026-008-АИ · лист 4 общих данных (продолжение)

## Условные обозначения

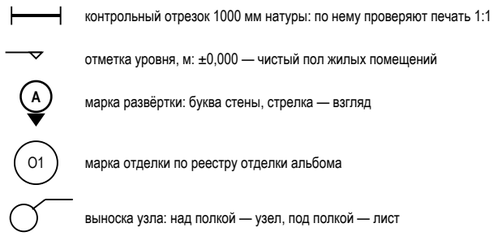


контрольный отрезок 1000 мм натуры: по нему проверяют печать 1:1

отметка уровня, м: ±0,000 — чистый пол жилых помещений

марка развёртки: буква стены, стрелка — взгляд

марка отделки по реестру отделки альбома

выноска узла: над полкой — узел, под полкой — лист

## Общие указания

1. Рабочие чертежи интерьера разработаны на основании задания на проектирование и обмерного плана (лист 12). Объект: Квартира с кабинетом; автор проекта — Кырлан Александр Сергеевич; общая площадь 127,29 м², жилая 92,29 м², помещений 9.
2. Рабочие чертежи выполнены в соответствии с заданием на проектирование и нормативными документами, перечисленными в п. 4.
3. Открытые вопросы, принятые допущения и конфликты между разделами, не снятые к выпуску комплекта, сведены в таблицы на листе 6. До ответа по пункту таблицы показанное на указанном там листе — допущение, а не утверждённое решение: комплект по этим листам предварительный.
4. Нормативные документы, на которые есть ссылки в листах комплекта: ГОСТ Р 21.101-2026; ГОСТ 21.501-2018; ГОСТ 2.302-68; ГОСТ 2.303-68; ГОСТ 2.304-81; ГОСТ 2.307-2011; СП 54.13330.2022; СП 71.13330.2017; СП 73.13330.2016; ПУЭ (7-е изд.), гл. 1.8, 7.1; ГОСТ Р 50571.7.701-2024; СанПиН 1.2.3685-21; ГОСТ 2.702; ГОСТ 2.755; ГОСТ 21.110-2013; ГОСТ 21.601; ГОСТ 13996-2019; ГОСТ 23166-2021; ГОСТ 31565-2012; ГОСТ 31975; ГОСТ 32414-2013; ГОСТ 32415-2013; ГОСТ Р 56387-2018; СП 29.13330.2011; СП 30.13330.2020; СП 51.13330.2011; СП 52.13330.2016. Документы из ведомости ссылочных документов здесь не повторяются.
5. За отметку ±0,000 принят уровень чистого пола жилых помещений квартиры (относительная отметка; абсолютная — по проекту дома). Отметка чистого пола мокрых помещений — −0,015. Размеры — в миллиметрах, отметки — в метрах, площади — в м²; высоты установки Н от чистого пола своего помещения до оси изделия.
6. Несущие конструкции, общедомовые стояки, вентиляционные каналы и инженерные сети дома настоящим комплектом не изменяются. Работы, затрагивающие их (проём или штраба в несущей стене, перенос стояка, врезка в вентканал, расширение мокрой зоны), выполняются только по отдельному проекту, к которому прилагается техническое заключение о допустимости и безопасности работ, выданное автором проекта дома или организацией с допуском на обследование, и который согласован в установленном порядке (Жилищный кодекс РФ, ст. 25–29).
7. Трассы инженерных сетей на листах — принципиальные. Расчёты электрических нагрузок и токов КЗ, гидравлики, воздухообмена, освещённости и нагрузок на перекрытие выполняются в проектах ЭОМ, ВК, ОВ и КР организацией с допуском СРО; фактические трассы до закрытия отделкой фиксируются исполнительными схемами.
8. Стиль интерьера — Модерн (ар-нуво) 60 % + Современный (контемпорари) 40 %. Палитра проекта: основной 60 % — Farrow & Ball No. 15 «Bone — мягкий каменно-серый с зеленцой», NCS S 2010-Y30R «Тёплый льняной беж», Tikkurila V503 «Winter»; дополнительный 30 % Farrow & Ball No. 34 «Calke Green — традиционный шалфей», Farrow & Ball No. 286 «Peignoir — серо-розовый»; акцент 10 % — NCS S 5030-B10G «Павлиний сине-зелёный», Farrow & Ball No. 66 «India Yellow — глубокая горчица», NCS S 8010-Y30R «Тёмно-коричневый». Коды цвета — по веерам производителей; цвет утверждается по выкрасу на объекте при освещении проекта.
9. Площади поверхностей — по чистым граням стен до отделки: стены = периметр × высоту от чистого пола помещения до низа потолка минус проёмы (облицовка плиткой — до верха облицовки); плинтус = периметр минус дверные проёмы; пол и потолок — по площади помещения. Количество плиток — по раскладке. Способ один для всех листов комплекта (ведомость отделки, колерная карта, раскладка плитки, развёртки).
10. Марки: стены помещения на всех листах — А (верхняя по плану), Б (правая), В (нижняя), Г (левая); марка отделки О — одна на весь альбом; реестр марок отделки (с позициями колерной карты той же отделки) и марки позиций по видам — на листе 61.
11. Развёртки стен выполнены по всем помещениям для стен с электроточками, мебелью, декором и отделкой: санузлы и кухонный фронт — в М 1:25, остальные стены — в М 1:40; расположение развёрток и узлов — на листе 62, узлы — на листе 85.
12. Перечень скрытых работ, на которые составляются акты освидетельствования (форма по приказу Минстроя России № 344/пр): гидроизоляция пола и стен мокрых помещений (с тестом проливом); стяжка пола (толщина, прочность, влажность основания); скрытая электропроводка (за потолком и в штробах стен; условия штробления — в следующем пункте); трубопроводы водоснабжения и канализации до закрытия (опрессовка, уклоны); закладные и усиления под подвесные приборы, мебель и тяжёлый декор, рамы инсталляций; короба дверей скрытого монтажа до штукатурки; каркасы ГКЛ потолков, коробов и перегородок до обшивки.
13. Скрытая электропроводка: за потолком и в штробах стен. Штробы в стенах выполняются только после технического заключения о несущих конструкциях; до заключения несущие стены не определены, и все стены считаются несущими; объём штроб — в ведомости объёмов работ, строка «Штробы в стенах» (вертикальные спуски; объём не меньше фактического, горизонтальные трассы — по исполнительной схеме).
14. Критерии приёмки: допуски отделочных покрытий — по СП 71.13330.2017; испытания систем водоснабжения и канализации — по СП 73.13330.2016 до закрытия трасс; приёмо-сдаточные испытания электроустановки — по ПУЭ, гл. 1.8, с протоколом электролаборатории.
15. Осознанные отступления от ГОСТ Р 21.101-2026, принятые в комплекте: номер листа и число листов («Листов») указаны на каждом листе; на масштабных листах в основной надписи указан фактический масштаб и дан контрольный отрезок 1000 мм; развёртки стен выполнены в М 1:25 и 1:40 (ГОСТ 21.507-81 — 1:50…1:500) ради читаемости привязок; размерные числа и марки элементов (Д-1, ОК-1, О6) — кеглем 2,5 мм, номера помещений — в кружке Ø 8 мм (канон — 3,5 мм и Ø 12 мм): так насыщенные листы А3 читаются без наложений надписей.
16. Графы «Пров.», «Н. контр.», «Утв.» основной надписи заполняются при согласовании комплекта с заказчиком; до согласования комплект подписывает автор проекта (графа «Разраб.»).

**Допущения и предложения на листе**

Основа листа: размеры сняты с растрового плана заказчика с частичными размерами: рисунок не в масштабе, помещения выровнены по подписанным размерам мебели и проходов; контрольный обмер не выполнен (К-1); высота потолка 2700 мм принята: на плане заказчика её нет (К-2); толщины стен 300 / 120 мм приняты по плану заказчика, не замерены (К-1); разрешённая мощность 15 кВт принята по типовым ТУ для квартиры, ТУ заказчиком не переданы (К-4).
См. лист открытых вопросов (лист 6, записи К-1, К-2, К-4).

| | | | | | | | | |
|---|---|---|---|---|---|---|---|---|
| | | | | | | **ГД-2026-008-АИ** | | |
| | | | | | | Квартира с кабинетом<br>Общая площадь 127,29* м² · * размеры со скана, не замерены (реестр — л. 6, К-1) | | |
| Изм. | Кол.уч | Лист | № док. | Подп. | Дата | | | |
| Разраб. | | Кырлан А.С. | | | 18.10.26 | Дизайн-проект интерьера | Стадия: РП | Лист: 5 / Листов: 92 |
| Пров. | | | | | | | | |
| ГИП | | | | | | | | |
| | | | | | | **Общие данные**<br>М б/м | **Кырлан Александр Сергеевич** | |
| Н. контр. | | | | | | | | |
| Утв. | | | | | | | | |

выпуск 18.10.2026 № d2d5a25dca · стр. 7 из 129

# Открытые вопросы, принятые допущения и конфликты

Сводка по реестрам координации (стартовое совещание 18.10.2026)

Комплект предварительный по пунктам этих таблиц. Пока по пункту нет ответа или решения, показанное на указанном листе — допущение проектировщика, а не утверждённое решение.
Сводка: открытых вопросов — 4 (из них ждут факта объекта — 2: контрольного обмера, обследования или документа).
Пункты, ответ на которые лежит на объекте, а не за столом проектировщика (графа «Вид», строка «Ждёт»), собраны на листе «Задание на контрольный обмер и обследование» (листы 7, 8): что и где замерить, с какой точностью и чем подтвердить. Пункты, ждущие решения человека, на объекте не закрываются.

## Открытые вопросы и принятые допущения

| № | Формулировка | Вид | Кто решает | Если решения нет | Лист, где это проявляется |
|---|---|---|---|---|---|
| К-1 | Размеры квартиры сняты с растрового плана заказчика с частичными размерами (рисунок не в масштабе): помещения выровнены по подписанным размерам мебели и проходов. До заказа мебели, дверей и материалов нужен контрольный обмер всех помещений и проёмов. | Отсутствует<br>Ждёт: обмера | Архитектор-планировщик | размеры на листах — по плану заказчика, уточняются по месту; мебель на заказ и материалы по ним не заказывать | л. 12 — Обмерный план<br>л. 16 — План расстановки мебели |
| К-2 | Высота потолка на плане заказчика не указана, принята 2700 мм. | Отсутствует | Архитектор-планировщик | высоты на развёртках и потолки — от 2700 мм, уточнить при обмере | л. 12 — Обмерный план<br>л. 34 — План потолков |
| К-4 | Разрешённая мощность квартиры по ТУ неизвестна, принята 15 кВт. | Отсутствует | Инженер-электрик | щит и группы рассчитаны на 15 кВт; при меньших ТУ пересчёт | л. 25 — Однолинейная схема щита<br>л. 20 — План розеток и электровыводов |
| К-5 | Перепланировка (гардеробная-постирочная при спальне, Г-образный коридор, широкий проём прихожая — гостиная, гостевой санузел у прихожей) — предложение проектировщика: несущие стены дома неизвестны. Нужны поэтажный план БТИ / техзаключение и решение заказчика. | Отсутствует<br>Ждёт: документа | Архитектор-планировщик | перегородки и проёмы — предложение, к строительству не выдаются; мокрые зоны и кухня оставлены на местах плана заказчика | л. 12 — Обмерный план |

## Примечания

1. Номера листов — по ведомости рабочих чертежей комплекта (лист «Общие данные»).
2. Графа «Если решения нет» показывает состояние решения на листах; влияние на сроки и стоимость по пунктам не оценивалось.
3. Пункт, по которому принято решение, при следующем выпуске комплекта из таблиц исключается.

| Изм. | Кол.уч | Лист | № док. | Подп. | Дата | ГД-2026-008-АИ | | |
|---|---|---|---|---|---|---|---|---|
| | | | | | | Квартира с кабинетом<br>Общая площадь 127,29* м² · * размеры со скана, не замерены (реестр — л. 6, К-1) | | |
| Разраб. | | Кырлан А.С. | | | 18.10.26 | Дизайн-проект интерьера | Стадия: РП | Лист: 6 / Листов: 92 |
| Пров. | | | | | | | | |
| ГИП | | | | | | | | |
| Н. контр. | | | | | | **Открытые вопросы, принятые допущения и конфликты**<br>М б/м | **Кырлан Александр Сергеевич** | |
| Утв. | | | | | | | | |

# Задание на контрольный обмер и обследование. Лист 1 из 2

**ПРЕДВАРИТЕЛЬНО · не для производства работ · открыто пунктов: 4 (реестр — л. 6)**

Что замерить, вскрыть и получить до заказа материалов и изделий

Задание собрано из открытых вопросов, ответ на которые лежит на объекте или в документах, а не за столом проектировщика. Пока факт не получен, размер, материал или положение на листах — допущение (знак «*»), а не замер.
Сводка: на объекте — 7 (до демонтажа — 5; после демонтажа — 2); документом и при закупке — 2; из допущений в данных и на листах — 8, из них без вопроса в реестре — 5. Закрываются вопросы: К-1, К-2, К-4, К-5 (4). Вопросы, ждущие решения человека, задание не закрывает — они решаются по реестру открытых вопросов.

## Условия проведения

| Порядок работ | Приёмы и точность | Кто присутствует | Если факт не совпал с проектом |
|---|---|---|---|
| 1. До демонтажа — существующее состояние: контур, диагонали, высоты, проёмы, оси стояков, ниши и конструкции, которые видны.<br>2. После демонтажа, до черновых работ — то, что закрывали отделка и короба: основание стен, фактические толщины, углы, узлы.<br>3. Документы и данные закупки — не на объекте: к сроку из последней таблицы, от них зависят привязки и заказ.<br>Что заказывается по размеру из задания, до закрытия пункта не заказывают: сроки изготовления — по графику закупок прораба. | Обход по часовой стрелке от входа: стены, проёмы, потолок, коммуникации (стояки, щиток, вентканалы), особенности (ниши, короба, выступы).<br>Размеры записывают в мм; сумма участков равна общему размеру, при цепочке длиннее трёх участков ставят проверочный (общий) размер.<br>Диагонали каждого помещения; если две диагонали различаются на 5 мм и больше, разницу подписывают на плане.<br>Потолок — в нескольких точках: центр, углы, у проёмов. Проём — ширина, высота, глубина откоса, привязка к ближайшим углам, высота подоконника.<br>Допустимая погрешность прибора — 2–3 мм на метр; размеры округляют кратно 5 мм; два контрольных промера одного размера не должны расходиться более чем на 2 %. Допуск по пункту — в графе «Точность».<br>План БТИ обмер не заменяет. | Прораб (отвечает за проведение) — назначает день и порядок обхода, открывает объект и освобождает помещения, ведёт это задание и реестр изменений.<br>Архитектор — выполняет обмер, составляет акт контрольного обмера и подписывает результаты по размерам и конструкциям.<br>Владельцы вопросов присутствуют при пунктах своего раздела или принимают результат до заказа: Инженер ВК (вода, канализация) позиции О-1; Инженер-электрик — К-4; позиции О-2; Инженер ОВ позиции О-3; Отделочник — позиции О-6, О-7.<br>Заказчик или его представитель — передаёт документы (план БТИ, проект дома, технические условия, паспорта), подписывает акт. Проектных решений на обмере не принимают: обмер даёт факт, решения — по реестру открытых вопросов (лист 6). | 1. В пределах допуска пункта — принимается измеренное значение, лист перевыпускается, знак «*» снимается.<br>2. Больше допуска или контрольные промеры расходятся более чем на 2 % — промер повторяют; не подтвердилось — запись в реестр изменений (дата, лист, было, стало, кто решил, подпись), работы в этом месте не начинают.<br>3. Затронуты несущая стена, стояк, вентканал или мокрая зона — сразу владельцу раздела и ГИПу (главному инженеру проекта); между разделами не больше двух кругов, затем решает ГИП.<br>4. На объекте устно ничего не согласуется: каждое решение — записью в реестр с подписью. |

## Этап 1. До демонтажа

| № | Где | Способ | Что сделать | Кто выполняет | Точность | Что пересчитается в альбоме | Чем подтверждается | Закрывает вопросы реестра |
|---|---|---|---|---|---|---|---|---|
| О-1 | Ввод В1 и Т3 у стояков; по всей квартире | Обмер | Отключающая арматура и счётчики воды на вводах: положение, тип, пломбы управляющей компании. Альбом ставит их на каждом вводе по практике, в данных их нет. | Архитектор | ±5 мм | Узлы ввода в спецификации ВК (краны, фильтры, счётчики); места ввода на плане выводов.<br>Листы:<br>л. 30 — План выводов сантехники<br>л. 32 — Спецификация сантехнического оборудования | акт контрольного обмера; фото с рулеткой и привязкой к стене или углу | Вопроса в реестре нет: Альбом принимает счётчики воды на вводах без осмотра.<br>Результат принимает: Инженер ВК (вода, канализация) |
| О-2 | Вход в квартиру или лестничная клетка; место щита на плане | Обмер | Существующий щиток и счётчик электроэнергии: место и габарит ниши, состояние ввода, марка и сечение вводного кабеля, наличие вводного автомата и УЗО, пломбы. | Архитектор | ±5 мм | Ниша и место щита на листах; вводной кабель и аппараты на однолинейной схеме; расстояния до первых групп.<br>Листы:<br>л. 25 — Однолинейная схема щита | акт контрольного обмера; фото с рулеткой и привязкой к стене или углу | Вопроса в реестре нет: Альбом принимает щит и ввод без осмотра.<br>Результат принимает: Инженер-электрик |
| О-3 | Спальня (пом. 1), Кабинет (пом. 3), Кухня-гостиная (пом. 4), Детская (пом. 6); у окон | Обмер | Положение стояков отопления (подающий и обратный) от граней стен, диаметры, наличие запорной арматуры; существующие радиаторы: число секций, межосевое расстояние, подводки. В данных стояков отопления нет — лист отопления выводит их условно у откоса окна, радиаторы — «принципиально, по расчёту». | Архитектор | ±5 мм | План отопления: места стояков и подводок, привязки радиаторов; подбор радиаторов по теплотехническому расчёту; радиаторы и узлы подключения в ВОР и спецификации.<br>Листы:<br>л. 29 — План отопления | акт контрольного обмера; фото с рулеткой и привязкой к стене или углу | Вопроса в реестре нет: Альбом принимает положение стояков и радиаторов отопления без обмера.<br>Результат принимает: Инженер ОВ |
| О-4 | все помещения | Обмер | Контрольный обмер всех помещений: стороны, диагонали, проёмы, высота потолка. | исполнитель | ±5 мм; диагонали — разница от 5 мм подписывается | обмерный и монтажный планы, развёртки, мебель на заказ<br>Листы:<br>л. 12 — Обмерный план<br>л. 16 — План расстановки мебели | акт контрольного обмера | К-1<br>Результат принимает: Архитектор |

**Допущения и предложения на листе**
Основа листа: размеры сняты с растрового плана заказчика с частичными размерами: рисунок не в масштабе, помещения выровнены по подписанным размерам мебели и проходов; контрольный обмер не выполнен (К-1); высота потолка 2700 мм принята: на плане заказчика её нет (К-2); толщины стен 300 / 120 мм приняты по плану заказчика, не замерены (К-1); разрешённая мощность 15 кВт принята по типовым ТУ для квартиры, ТУ заказчиком не переданы (К-4).
См. лист открытых вопросов (лист 6, записи К-1, К-2, К-4).

| Изм. | Кол.уч | Лист | № док. | Подп. | Дата |
|---|---|---|---|---|---|
| Разраб. | | Кырлан А.С. | | | 18.10.26 |
| Пров. | | | | | |
| ГИП | | | | | |
| | | | | | |
| Н. контр. | | | | | |
| Утв. | | | | | |

**ГД-2026-008-АИ**

Квартира с кабинетом

Общая площадь 127,29* м² · * размеры со скана, не замерены (реестр — л. 6, К-1)

Дизайн-проект интерьера

| Стадия | Лист | Листов |
|---|---|---|
| РП | 7 | 92 |

**Задание на контрольный обмер и обследование.**
**Лист 1 из 2**
М б/м

**Кырлан Александр Сергеевич**

выпуск 18.10.2026 № d2d5a25dca · стр. 9 из 129

# Задание на контрольный обмер и обследование. Лист 2 из 2

**ПРЕДВАРИТЕЛЬНО · не для производства работ · открыто пунктов: 4 (реестр — л. 6)**

Что замерить, вскрыть и получить до заказа материалов и изделий

### Этап 1. До демонтажа (продолжение)

| № | Где | Способ | Что сделать | Кто выполняет | Точность | Что пересчитается в альбоме | Чем подтверждается | Закрывает вопросы реестра |
|---|---|---|---|---|---|---|---|---|
| О-5 | Все помещения квартиры | Обмер | Высота потолка в каждом помещении в нескольких точках: центр, углы, у проёмов. | Архитектор | ±5 мм | Вертикальные размеры альбома: развёртки, шкафы, плитка, объёмы работ.<br>Листы:<br>л. 2–5 — Общие данные | акт контрольного обмера | К-2<br>Результат принимает: Архитектор |

### Этап 2. После демонтажа, до черновых работ

| № | Где | Способ | Что сделать | Кто выполняет | Точность | Что пересчитается в альбоме | Чем подтверждается | Закрывает вопросы реестра |
|---|---|---|---|---|---|---|---|---|
| О-6 | Спальня (пом. 1), Гардеробная-постирочная (пом. 2), Кабинет (пом. 3), Кухня-гостиная (пом. 4), Коридор (пом. 5), Детская (пом. 6), Ванная (пом. 7), Прихожая (пом. 8), Санузел гостевой (пом. 9) | Обмер | Нивелировка плиты перекрытия и существующего пола после демонтажа покрытий: отметки в углах и по сетке, перепады по помещению, уклоны, отметки порогов (чистый пол в мокрых зонах принят -15 мм, 0 мм). Принятая толщина стяжки 33 мм, 50 мм и отметка чистого пола — расчётные, не от замера плиты. | Архитектор | ±5 мм по отметке; ровность просвет под 2-метровой рейкой, горизонталь против 0,2 % длины помещения | Толщина стяжки и отметка чистого пола; уклоны к трапам и пороги; выпуски К1 относительно чистого пола (план разводки); объёмы стяжки и смеси в ВОР и спецификации.<br>Листы:<br>л. 35, 39 — План полов<br>л. 31 — Схема разводки водопровода и канализации | акт контрольного обмера | Вопроса в реестре нет: Альбом принимает отметки плиты и толщину пирога пола без нивелировки.<br>Результат принимает: Отделочник |
| О-7 | Спальня (пом. 1), Гардеробная-постирочная (пом. 2), Кабинет (пом. 3), Кухня-гостиная (пом. 4), Коридор (пом. 5), Детская (пом. 6), Ванная (пом. 7), Прихожая (пом. 8), Санузел гостевой (пом. 9) | Обмер | Вертикаль и плоскостность стен: отклонение от вертикали по высоте стены (отвес или лазерный уровень), просвет под правилом 2 м, кривизна углов. Нужно там, где от стены зависит изделие: облицовка плиткой (пом. 7, 9), штукатурка и окраска (пом. 1, 2, 3, 4, 5, 6, 7, 8, 9), встроенная мебель и кухня (пом. 3, 4, 6, 8). | Архитектор | до 1 мм на 2 м (правило и клиновой щуп); вертикаль — мм на высоту стены, отклонения подписываются на плане | Толщина штукатурки и расход смеси в ВОР и спецификации; раскладка плитки (подрезка у стен); зазоры и крепление встроенной мебели и кухни.<br>Листы:<br>л. 35–38 — Раскладка плитки<br>л. 40, 41 — Ведомость отделки помещений | акт контрольного обмера | Вопроса в реестре нет: Альбом принимает стены ровными и вертикальными без замера.<br>Результат принимает: Отделочник |

### Документы и данные закупки (не на объекте)

| № | У кого, откуда | Способ | Что получить | К какому сроку | Что пересчитается в альбоме | Чем подтверждается | Закрывает вопросы реестра |
|---|---|---|---|---|---|---|---|
| О-8 | Заказчик; организация, выдавшая технические условия | Документ | Технические условия на присоединение: разрешённая мощность. | До утверждения однолинейной схемы щита | Однолинейная схема щита: вводной аппарат и группы.<br>Листы:<br>л. 2–5 — Общие данные | копия документа | К-4<br>Результат принимает: Инженер-электрик |
| О-9 | вся квартира | Документ | Поэтажный план БТИ и техническое заключение о несущих стенах. | до демонтажа и возведения перегородок | монтажный план, проёмы, развёртки<br>Листы:<br>л. 12 — Обмерный план | копия документа | К-5<br>Результат принимает: Архитектор |

### Примечания

1. Подтверждение: акт контрольного обмера (дата, кто присутствовал, прибор, перечень промеров с результатами, подписи присутствующих); к акту — фото вскрытий и узлов и техническое заключение организации, выполнившей обследование.
2. Номера листов — по ведомости рабочих чертежей комплекта (лист «Общие данные»).
3. Пункт исключается из задания при следующем выпуске, когда акт подписан, значение внесено в проект и листы перевыпущены; знак «*» у величины снимается только замером.

**Допущения и предложения на листе**

Основа листа: размеры сняты с растрового плана заказчика с частичными размерами: рисунок не в масштабе, помещения выровнены по подписанным размерам мебели и проходов; контрольный обмер не выполнен (К-1); высота потолка 2700 мм принята: на плане заказчика её нет (К-2); толщины стен 300 / 120 мм приняты по плану заказчика, не замерены (К-1); разрешённая мощность 15 кВт принята по типовым ТУ для квартиры, ТУ заказчиком не переданы (К-4).
См. лист открытых вопросов (лист 6, записи К-1, К-2, К-4).

| Изм. | Кол.уч | Лист | № док. | Подп. | Дата |
|---|---|---|---|---|---|
| Разраб. | | Кырлан А.С. | | | 18.10.26 |
| Пров. | | | | | |
| ГИП | | | | | |
| | | | | | |
| Н. контр. | | | | | |
| Утв. | | | | | |

**ГД-2026-008-АИ**

Квартира с кабинетом

Общая площадь 127,29* м² · * размеры со скана, не замерены (реестр — л. 6, К-1)

Дизайн-проект интерьера

| Стадия | Лист | Листов |
|---|---|---|
| РП | 8 | 92 |

**Задание на контрольный обмер и обследование.**
**Лист 2 из 2**
М б/м

**Кырлан Александр Сергеевич**

выпуск 18.10.2026 № d2d5a25dca · стр. 10 из 129

# График закупок и работ. Лист 1 из 3

**ПРЕДВАРИТЕЛЬНО · не для производства работ · открыто пунктов: 4 (реестр — л. 6)**

Что заказывать и когда не раньше чего: относительный порядок без дат; срок поставки — из данных или «уточняется у поставщика»

Лист не содержит дат: контрольного обмера, подписанных решений автора и договоров ещё нет, и любая дата была бы выдумана. Вместо календаря — порядок и условия: замер → решение и выбор изделия → заказ → срок поставки → работа, которую позиция блокирует. Срок поставки печатается как срок, только если он задан в данных позиции. Нет — «срок уточняется у поставщика» и ссылка на вопрос реестра о сроках; типовой диапазон практики стоит рядом как ориентир и заказывать по нему нельзя. Номера З-N и Р-N — строки этого листа, К-N — записи реестра открытых вопросов, О-N — позиции задания на контрольный обмер.

## Закупки: что заказывается, от чего зависит заказ и какую работу блокирует

| № | Позиция и где | 1. Замер до заказа | 2. Решение, выбор изделия, паспорт | 3. Условие заказа | 4. Срок поставки | 5. Блокирует работу | Закрывает вопросы реестра |
|---|---|---|---|---|---|---|---|
| З-1 | Двери скрытого монтажа с коробом под покраску в существующих проёмах: Д-2, Д-3, Д-4, Д-5, Д-6, Д-7 — 6 шт.<br>пом. 1, 2, 3, 6, 7, 8 | О-4: обмер: все помещения (К-1); до заказа мебели и дверей | | После 1 и 2 и после получения срока у поставщика (вопроса о сроках нет); дата заказа — когда срок известен, не позднее чем за срок до начала Р-5. | срок уточняется у поставщика<br>Ориентир практики (не срок поставщика): ≈ 30 дн. | Р-5 «штукатурка»: короб ставят до штукатурки (коробку ставят на черновой стадии; полотно навешивают после чистовой отделки стен) | К-1 |
| З-2 | Кухонный гарнитур по проекту кухни: модули Кх1, Кх2, Кх3, Кх4, Кх5<br>пом. 4 | | | После 1 и 2 и после получения срока у поставщика (вопроса о сроках нет); дата заказа — когда срок известен, не позднее чем за срок до начала Р-15. | срок уточняется у поставщика<br>Ориентир практики (не срок поставщика): 4–8 нед. от замера | Р-15 «кухня и мебель»: замер кухни — по готовым стенам после штукатурки или плитки, до чистового пола; производство идёт параллельно со стяжкой и отделкой | |
| З-3 | Встраиваемая техника кухни: Кх1 холодильник, Кх3 посудомоечная машина, Кх5 oven<br>пом. 4 | | | После 1 и 2 и после получения срока у поставщика (вопроса о сроках нет); дата заказа — когда срок известен, не позднее чем за срок до начала Р-15. | срок уточняется у поставщика | Р-15 «кухня и мебель»: паспорта и монтажные схемы — до изготовления модулей кухни: нишу и вентзазоры задаёт модель, а не типовая схема 60 см | |
| З-4 | Стиральная машина: П6 (вертикальная загрузка 400 × 600 мм — условие закупки)<br>пом. 7 | | | После 1 и 2 и после получения срока у поставщика (вопроса о сроках нет); дата заказа — когда срок известен, не позднее чем за срок до начала Р-4. | срок уточняется у поставщика | Р-4 «черновая сантехника»: габарит и подводка — до закрытия люка и разводки | |
| З-5 | Сантехнические приборы и инсталляции: П1, П2, П3, П4, П10, П11, П12<br>пом. 7, 9 | О-3: обмер: Спальня (пом. 1), Кабинет (пом. 3), Кухня-гостиная (пом. 4), Детская (пом. 6); у окон | | После 1 и 2 и после получения срока у поставщика (вопроса о сроках нет); дата заказа — когда срок известен, не позднее чем за срок до начала Р-4. | срок уточняется у поставщика | Р-4 «черновая сантехника»: инсталляцию ставят до обшивки ГКЛВ и до гидроизоляции стены | |
| З-6 | Керамогранит и плитка: 4 поз. по артикулу и формату, 68,96 м² по раскладке<br>пом. 4, 7, 8, 9 | О-6: обмер: Спальня (пом. 1), Гардеробная-постирочная (пом. 2), Кабинет (пом. 3), Кухня-гостиная (пом. 4), Коридор (пом. 5), Детская (пом. 6), Ванная (пом. 7), Прихожая (пом. 8), Санузел гостевой (пом. 9)<br>О-7: обмер: Спальня (пом. 1), Гардеробная-постирочная (пом. 2), Кабинет (пом. 3), Кухня-гостиная (пом. 4), Коридор (пом. 5), Детская (пом. 6), Ванная (пом. 7), Прихожая (пом. 8), Санузел гостевой (пом. 9) | | После 1 и 2 и после получения срока у поставщика (вопроса о сроках нет); дата заказа — когда срок известен, не позднее чем за срок до начала Р-9. | срок уточняется у поставщика | Р-9 «плитка»: калибр партии измеряют до раскладки, раскладку пересчитывают до заказа | |
| З-7 | Покрытие пола (доска) и плинтус: пом. 1, 2, 3, 4, 5, 6<br>пом. 1, 2, 3, 4, 5, 6 | О-6: обмер: Спальня (пом. 1), Гардеробная-постирочная (пом. 2), Кабинет (пом. 3), Кухня-гостиная (пом. 4), Коридор (пом. 5), Детская (пом. 6), Ванная (пом. 7), Прихожая (пом. 8), Санузел гостевой (пом. 9) | | После 1 и 2 и после получения срока у поставщика (вопроса о сроках нет); дата заказа — когда срок известен, не позднее чем за срок до начала Р-12. | срок уточняется у поставщика | Р-12 «чистовые полы»: артикул и партия — до заказа; доску привозят к чистовым полам | |
| З-8 | Встроенная мебель по замеру цеха: К1, Кх13, Д1, П8<br>пом. 3, 4, 6, 8 | О-4: обмер: все помещения (К-1); до заказа мебели и дверей | | После 1 и 2 и после получения срока у поставщика (вопроса о сроках нет); дата заказа — когда срок известен, не позднее чем за срок до начала Р-15. | срок уточняется у поставщика<br>Ориентир практики (не срок поставщика): 4–8 нед. от замера | Р-15 «кухня и мебель»: цех замеряет по готовым стенам; производство 4–8 недель идёт параллельно с отделкой | К-1 |

**Допущения и предложения на листе**

Основа листа: размеры сняты с растрового плана заказчика с частичными размерами: рисунок не в масштабе, помещения выровнены по подписанным размерам мебели и проходов; контрольный обмер не выполнен (К-1); высота потолка 2700 мм принята: на плане заказчика её нет (К-2); толщины стен 300 / 120 мм приняты по плану заказчика, не замерены (К-1); разрешённая мощность 15 кВт принята по типовым ТУ для квартиры, ТУ заказчиком не переданы (К-4).
См. лист открытых вопросов (лист 6, записи К-1, К-2, К-4).

| Изм. | Кол.уч | Лист | № док. | Подп. | Дата |
|---|---|---|---|---|---|
| Разраб. | | Кырлан А.С. | | | 18.10.26 |
| Пров. | | | | | |
| ГИП | | | | | |
| | | | | | |
| Н. контр. | | | | | |
| Утв. | | | | | |

**ГД-2026-008-АИ**

Квартира с кабинетом

Общая площадь 127,29* м² · * размеры со скана, не замерены (реестр — л. 6, К-1)

Дизайн-проект интерьера

| Стадия | Лист | Листов |
|---|---|---|
| РП | 9 | 92 |

**График закупок и работ. Лист 1 из 3**

М б/м

**Кырлан Александр Сергеевич**

выпуск 18.10.2026 № d2d5a25dca · стр. 11 из 129

# График закупок и работ. Лист 2 из 3

**ПРЕДВАРИТЕЛЬНО · не для производства работ · открыто пунктов: 4 (реестр — л. 6)**

Что заказывать и когда не раньше чего: относительный порядок без дат; срок поставки — из данных или «уточняется у поставщика»

## Работы: порядок и что не даёт начать

| № | Работа (стадия технологической последовательности) | После | Что должно быть к началу: условия и закупки | Не начинать, пока открыто в реестре |
|---|---|---|---|---|
| Р-1 | Демонтаж покрытий, отделки стен и потолков, дверных блоков и приборов; конструкции, стены и перегородки не трогать до технического заключения (стадия 1) | | до начала: запрошены документы на дом и БТИ; контрольный обмер до демонтажа (что видно) сделан | |
| Р-2 | Контрольный обмер на голых стенах и обследование (задание — лист «Задание на контрольный обмер») (стадия 2) | Р-1 | после снятия отделки: видны стояки, каналы, щиток, толщины стен; до заказа всего, что делают по размеру | |
| Р-3 | Черновая электрика: штробы, короба, гофра, подрозетники, щит (стадия 4) | Р-2 | до начала: план электрики с высотами утверждён; штробы в стенах — только после технического заключения; мебель расставлена | К-4: Разрешённая мощность квартиры по ТУ неизвестна, принята 15 кВт. |
| Р-4 | Черновая сантехника и вентиляция: разводка, выводы, инсталляции, короба стояков (стадия 5) | Р-2 | до начала: положение стояков замерено; модели инсталляций и машины выбраны (габариты рамы, подводка); инсталляцию ставят до обшивки ГКЛВ и до гидроизоляции<br>Закупки к началу: З-4 (стиральная машина), З-5 (сантехника) | |
| Р-5 | Коробки скрытых дверей, затем штукатурка стен и откосов (стадия 6) | Р-2, Р-3, Р-4 | до начала: электрика и сантехника смонтированы, штробы заделаны; коробки скрытых дверей установлены до штукатурки (поэтому заказ дверей — раньше работы)<br>Закупки к началу: З-1 (двери скрытого монтажа) | К-1: Размеры квартиры сняты с растрового плана заказчика с частичными размерами (рисунок не в масштабе): помещения выровнены по подписанным размерам мебели и проходов. |
| Р-6 | Стяжка пола и тёплый пол (стадия 7) | Р-5 | до начала: штукатурка сделана; трубы под стяжкой приняты; нивелировка плиты выполнена | |
| Р-7 | Гидроизоляция санузлов и тест проливом (стадия 8) | Р-6 | до начала: стяжка набрала прочность и сухая по инструкции гидроизоляции; выводы стоят на проектных отметках | |
| Р-8 | ГКЛ: короба инсталляции и стояков, ниши, потолки (стадия 9) | Р-3, Р-4 | до начала: черновые сети в зоне коробов приняты; закладные под тяжёлое и карнизы стоят; светильники выбраны (вырезы) | |
| Р-9 | Плитка и керамогранит: стены, затем пол; фартук (стадия 10) | Р-6, Р-7, Р-8 | до начала: гидроизоляция принята; плитка выбрана, калибр партии измерен, раскладка пересчитана и подписана<br>Закупки к началу: З-6 (плитка) | |
| Р-10 | Шпаклёвка стен и потолков под окраску (стадия 11) | Р-5, Р-8, Р-9 | до начала: плитка готова (грязные работы закончены); штукатурка и ГКЛ сухие | |
| Р-11 | Окраска стен, потолков, откосов (стадия 13) | Р-10 | до начала: шпаклёвка отшлифована и огрунтована; выкрасы утверждены, колеровка одной партией | |
| Р-12 | Чистовые полы: инженерная доска (стадия 14) | Р-9, Р-11 | до начала: влажность основания в норме, мокрые работы закончены; доска выбрана и привезена<br>Закупки к началу: З-7 (доска и плинтус) | |
| Р-13 | Полотна межкомнатных дверей, плинтусы, пороги (стадия 15) | Р-11, Р-12 | до начала: чистовой пол уложен; полотна скрытых дверей — после чистовой отделки стен | |
| Р-14 | Чистовая электрика и сантехника: механизмы, светильники, смесители, приборы (стадия 16) | Р-11, Р-13 | до начала: отделка готова; механизмы, светильники и приборы выбраны и привезены | |
| Р-15 | Кухня, встроенная и корпусная мебель, бытовая техника (стадия 17) | Р-13, Р-14 | до начала: чистовая сантехника и электрика подведены к местам мебели; замер кухни снят по готовым стенам (после штукатурки или плитки, до чистового пола)<br>Закупки к началу: З-2 (кухонный гарнитур), З-3 (техника кухни), З-8 (мебель по замеру) | К-1: Размеры квартиры сняты с растрового плана заказчика с частичными размерами (рисунок не в масштабе): помещения выровнены по подписанным размерам мебели и проходов. |
| Р-16 | Сдача: осмотр по чек-листу, дефектная ведомость, устранение замечаний (стадия 18) | Р-14, Р-15 | до начала: всё смонтировано; акты скрытых работ подписаны | |

**Допущения и предложения на листе**

Основа листа: размеры сняты с растрового плана заказчика с частичными размерами: рисунок не в масштабе, помещения выровнены по подписанным размерам мебели и проходов; контрольный обмер не выполнен (К-1); высота потолка 2700 мм принята: на плане заказчика её нет (К-2); толщины стен 300 / 120 мм приняты по плану заказчика, не замерены (К-1); разрешённая мощность 15 кВт принята по типовым ТУ для квартиры, ТУ заказчиком не переданы (К-4).

См. лист открытых вопросов (лист 6, записи К-1, К-2, К-4).

| Изм. | Кол.уч | Лист | № док. | Подп. | Дата |
|---|---|---|---|---|---|
| Разраб. | | Кырлан А.С. | | | 18.10.26 |
| Пров. | | | | | |
| ГИП | | | | | |
| Н. контр. | | | | | |
| Утв. | | | | | |

**ГД-2026-008-АИ**

Квартира с кабинетом

Общая площадь 127,29* м² · * размеры со скана, не замерены (реестр — л. 6, К-1)

Дизайн-проект интерьера

| Стадия | Лист | Листов |
|---|---|---|
| РП | 10 | 92 |

**График закупок и работ. Лист 2 из 3**

М б/м

**Кырлан Александр Сергеевич**

выпуск 18.10.2026 № d2d5a25dca · стр. 12 из 129

# График закупок и работ. Лист 3 из 3

Что заказывать и когда не раньше чего: относительный порядок без дат; срок поставки — из данных или «уточняется у поставщика»

## Примечания

1. Порядок работ — стадии технологической последовательности из 16 позиций, присутствующих в этом проекте (по строкам ведомости объёмов); остальные стадии таблицы knowledge/remont-tehnologiya.md в проекте не встречаются. Длительности работ не печатаются: их нет ни в данных, ни в нормах для этого объекта.
2. Типовые сроки — ориентир практики, не срок поставщика: скрытые двери — короб около 10 дн., полотно под покраску до 3 нед., шпон 4–5 нед., в среднем около 30 дн. (knowledge/workers/foreman.md, п. 2.4 (profil-doors)); кухня и корпусная мебель — 4–8 недель от замера (knowledge/remont-tehnologiya.md, разд. 2; knowledge/workers/foreman.md, п. 2.4). Заказ по ориентиру не назначается: срок получают у поставщика (вопрос реестра), после чего заказ планируют «не позднее чем за срок до начала работы».
3. Условия заказа берутся из реестра открытых вопросов и задания на контрольный обмер: позиция заказывается, когда закрыты замер (графа 1) и решение (графа 2). Закрывать их может только факт или решение автора с подписью; снять строку с листа можно только закрыв запись реестра.
4. Заказ по размеру до контрольного обмера не делают: двери, кухня и встроенная мебель зависят от обмера (К-11, К-13); скрытые двери, кроме того, зависят от решения по нише санузла 2 (проём Д-5 в перегородке П-1).
5. Номера листов — по ведомости рабочих чертежей комплекта (лист «Общие данные»).

**Допущения и предложения на листе**

Основа листа: размеры сняты с растрового плана заказчика с частичными размерами: рисунок не в масштабе, помещения выровнены по подписанным размерам мебели и проходов; контрольный обмер не выполнен (К-1); высота потолка 2700 мм принята: на плане заказчика её нет (К-2); толщины стен 300 / 120 мм приняты по плану заказчика, не замерены (К-1); разрешённая мощность 15 кВт принята по типовым ТУ для квартиры, ТУ заказчиком не переданы (К-4).
См. лист открытых вопросов (лист 6, записи К-1, К-2, К-4).

| Изм. | Кол.уч | Лист | № док. | Подп. | Дата |
|---|---|---|---|---|---|
| Разраб. | | Кырлан А.С. | | | 18.10.26 |
| Пров. | | | | | |
| ГИП | | | | | |
| | | | | | |
| Н. контр. | | | | | |
| Утв. | | | | | |

**ГД-2026-008-АИ**

Квартира с кабинетом

Общая площадь 127,29* м² · * размеры со скана, не замерены (реестр — л. 6, К-1)

Дизайн-проект интерьера

| Стадия | Лист | Листов |
|---|---|---|
| РП | 11 | 92 |

**График закупок и работ. Лист 3 из 3**

М б/м

**Кырлан Александр Сергеевич**

выпуск 18.10.2026 № d2d5a25dca · стр. 13 из 129

01

# Архитектурные решения

Кырлан Александр Сергеевич

выпуск 18.10.2026 · d2d5a25dca · стр. 14 из 129

# Обмерный план

Существующее положение · размеры в мм · отметки от чистого пола

**ПРЕДВАРИТЕЛЬНО · не для производства работ · открыто пунктов: 4 (реестр — л. 6)**

## Отметки по высоте

| | |
|---|---|
| **±0,000** | чистый пол пом. 1–6, 8; отсчёт высот |
| **−0,015** | чистый пол пом. 7, 9, ниже на 15 мм |
| **−0,064*** | верх плиты — расчёт, не замер (задание на обмер) |
| **сущ. пол** | снимается до плиты; не замерен (задание на обмер) |

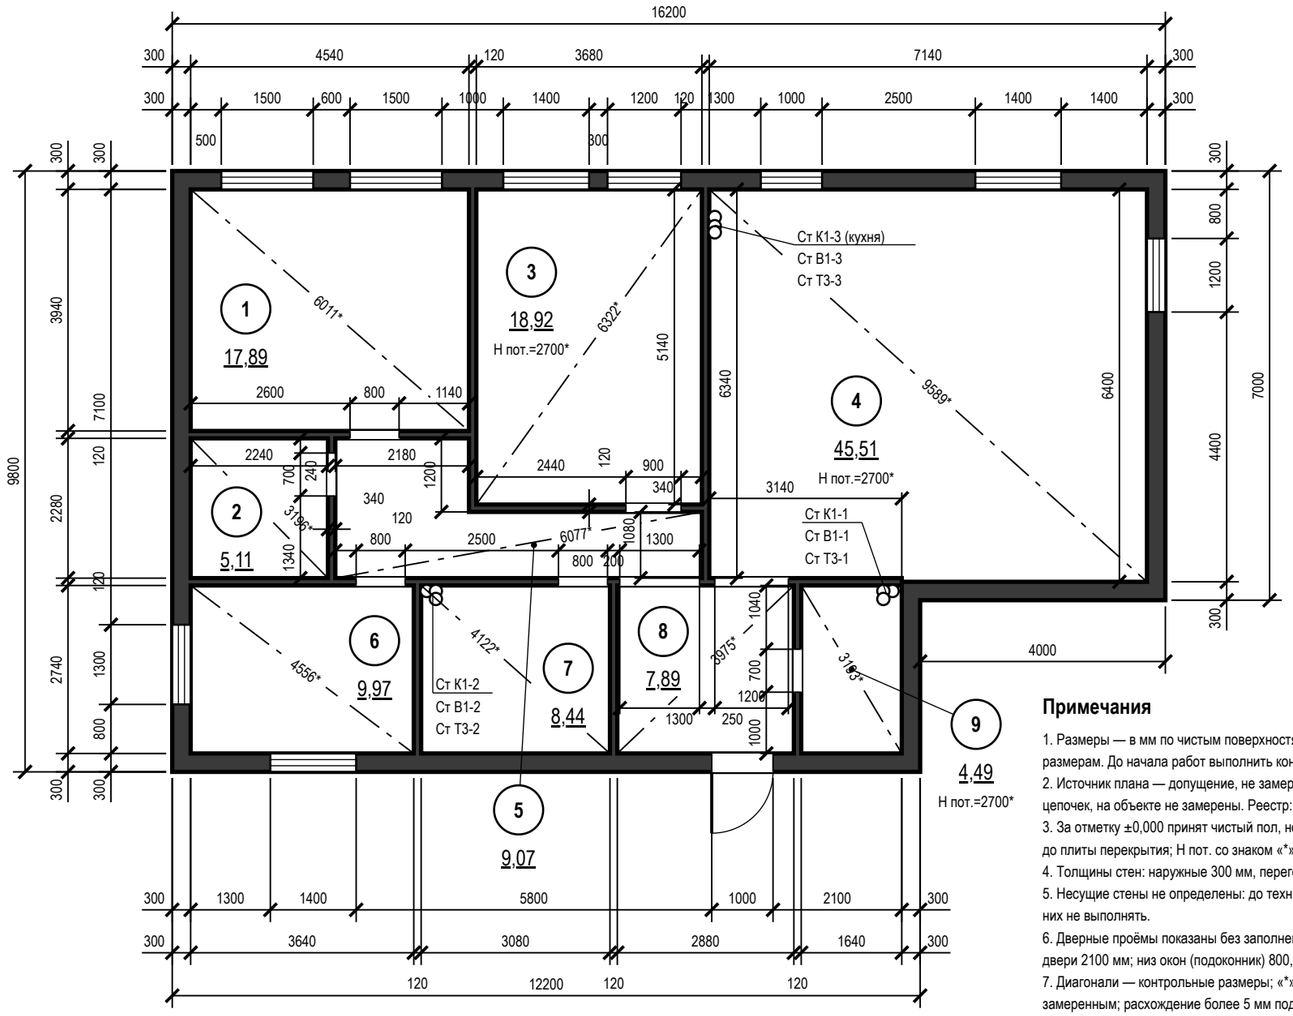


## Экспликация помещений

| № | Наименование | Площадь, м² |
|---|---|---|
| 1 | Спальня | 17,89 |
| 2 | Гардеробная-постирочная | 5,11 |
| 3 | Кабинет | 18,92 |
| 4 | Кухня-гостиная | 45,51 |
| 5 | Коридор | 9,07 |
| 6 | Детская | 9,97 |
| 7 | Ванная | 8,44 |
| 8 | Прихожая | 7,89 |
| 9 | Санузел гостевой | 4,49 |
| | **Итого (общая площадь)** | **127,29** |

## Условные обозначения

- существующие стены (сечение)
- окно (рама, остекление)
- проём существующий, без заполнения (откосы)
- стояк: К1 — канализация, В1 — ХВС, Т3 — ГВС
- диагональ помещения — контроль прямоугольности
- (1) номер помещения, площадь м²

## Принято, не определено или спорно

полностью — лист 6

К-5 — Перепланировка (гардеробная-постирочная при спальне, Г-образный коридор, широкий проём прихожая — гостиная, гостевой санузел у прихожей)

предложение проектировщика: несущие стены дома неизвестны

## Примечания

1. Размеры — в мм по чистым поверхностям стен до отделки (по плану заказчика); площади — в м² по тем же размерам. До начала работ выполнить контрольный обмер.
2. Источник плана — допущение, не замер: растровый скан плана заказчика, размеры сняты с размерных цепочек, на объекте не замерены. Реестр: лист 6, вопрос К-1.
3. За отметку ±0,000 принят чистый пол, не существующий (блок отметок). Н пот. — высота от чистого пола до плиты перекрытия; Н пот. со знаком «*» — принятая высота, не замер (вопрос К-2).
4. Толщины стен: наружные 300 мм, перегородки 120 мм; отличающиеся толщины и уступы — размерами на плане.
5. Несущие стены не определены: до технического заключения все стены считать несущими; проёмы и штробы в них не выполнять.
6. Дверные проёмы показаны без заполнения (двери — лист 14); высота дверных проёмов 2100 мм, проёмов без двери 2100 мм; низ окон (подоконник) 800, 1000, 900 мм от чистого пола, высота окон 1600, 1400 мм.
7. Диагонали — контрольные размеры; «*» — расчёт по принятому контуру (К-1), при обмере заменить замеренным; расхождение более 5 мм подписать на плане как перекос.
8. Размеры проверить на месте до начала работ; расхождение контрольных промеров ≤ 2 %.
9. Размеры короче 1 мм на листе цепочкой не показаны (две выносные линии на таком расстоянии сливаются): пом. 5, стена В — 40 мм от проёма до угла; пом. 8, стена А — 40 мм от угла до проёма; пом. 8, стена А 90 мм от проёма до угла.

**Допущения и предложения на листе**

Основа листа: размеры сняты с растрового плана заказчика с частичными размерами: рисунок не в масштабе, помещения выровнены по подписанным размерам мебели и проходов; контрольный обмер не выполнен (К-1); высота потолка 2700 мм принята: на плане заказчика её нет (К-2); толщины стен 300 / 120 мм приняты по плану заказчика, не замерены (К-1); разрешённая мощность 15 кВт принята по типовым ТУ для квартиры, ТУ заказчиком не переданы (К-4).

Открытые вопросы и конфликты по листу: К-1, К-2, К-5.

См. лист открытых вопросов (лист 6, записи К-1, К-2, К-4, К-5).

1000 мм · печать 1:1

| Изм. | Кол.уч | Лист | № док. | Подп. | Дата |
|---|---|---|---|---|---|
| Разраб. | | Кырлан А.С. | | | 18.10.26 |
| Пров. | | | | | |
| ГИП | | | | | |
| Н. контр. | | | | | |
| Утв. | | | | | |

**ГД-2026-008-АИ**

Квартира с кабинетом

Общая площадь 127,29* м² · * размеры со скана, не замерены (реестр — л. 6, К-1)

Дизайн-проект интерьера

| Стадия | Лист | Листов |
|---|---|---|
| РП | 12 | 92 |

**Обмерный план**

М 1:100

**Кырлан Александр Сергеевич**

выпуск 18.10.2026 № d2d5a25dca · стр. 15 из 129

# План демонтажа и монтажа перегородок

Перепланировка не выполняется · существующие стены сохраняются · размеры в мм

**ПРЕДВАРИТЕЛЬНО · не для производства работ · открыто пунктов: 4 (реестр — л. 6)**

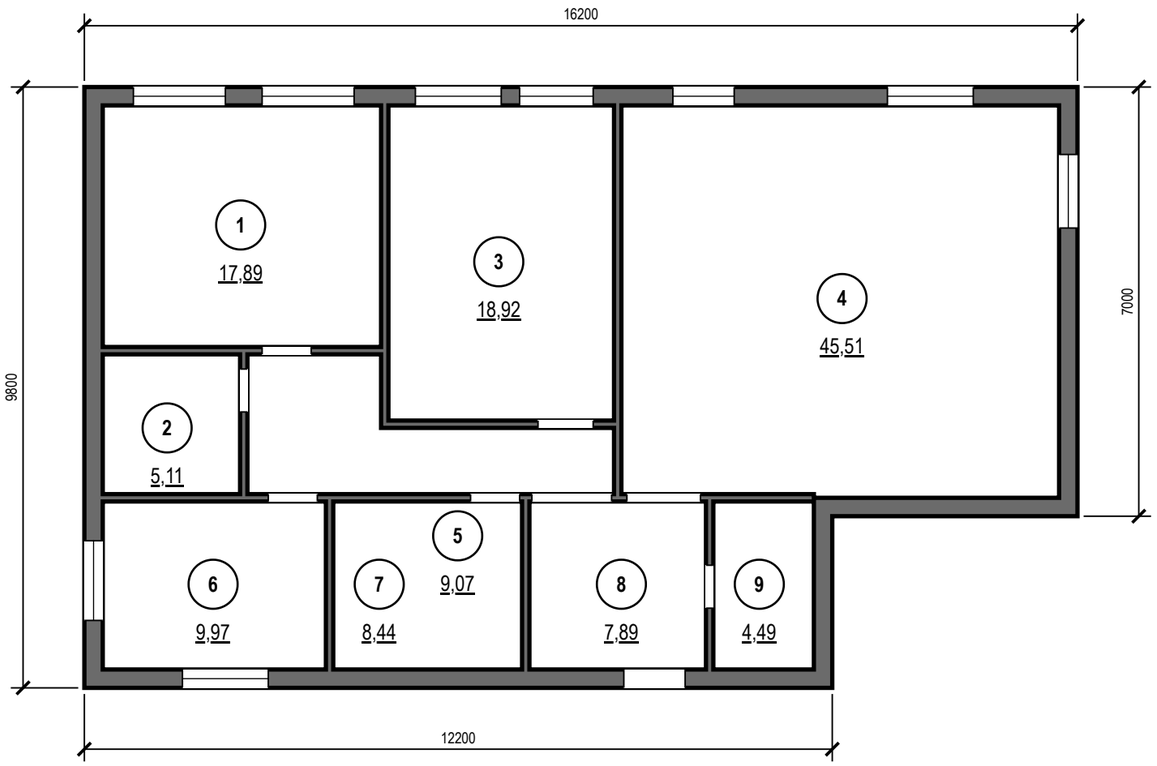


## Условные обозначения

- существующие стены — сохраняются;
- несущие не определены — считать несущими
- демонтируемые конструкции — на плане нет
- возводимые перегородки — на плане нет
- проём существующий, без заполнения (откосы)
- (1) номер помещения, площадь м²

## Отметки по высоте

| | | | |
|---|---|---|---|
| **±0,000** | чистый пол пом. 1–6, 8; отсчёт высот | **−0,064*** | верх плиты — расчёт, не замер (задание на обмер) |
| **−0,015** | чистый пол пом. 7, 9, ниже на 15 мм | **сущ. пол** | снимается до плиты; не замерен (задание на обмер) |

## Примечания

1. Перепланировка не выполняется: несущие и ненесущие стены, перегородки и плиты перекрытия не демонтируются, новые стены не возводятся; существующие стены и перегородки сохраняются.
2. Дверные блоки — по плану дверей (лист 14); существующие проёмы не расширяются.
3. Демонтаж существующих покрытий пола, стен и потолка, дверных блоков и сантехприборов (если есть) — до основания; объёмы демонтажа — для справки, по факту на объекте.
4. За отметку ±0,000 принят чистый пол, не существующий (блок отметок). Размеры — в мм по чистовой поверхности стен до отделки.
5. Размеры проверить на месте до начала работ: расхождение с обмером — не более 2 % (иначе — к архитектору).
6. Несущие стены не определены: до технического заключения все стены считать несущими — проёмы, ниши и штробы в них не выполнять.

**Допущения и предложения на листе**

Основа листа: размеры сняты с растрового плана заказчика с частичными размерами: рисунок не в масштабе, помещения выровнены по подписанным размерам мебели и проходов; контрольный обмер не выполнен (К-1); высота потолка 2700 мм принята: на плане заказчика её нет (К-2); толщины стен 300 / 120 мм приняты по плану заказчика, не замерены (К-1); разрешённая мощность 15 кВт принята по типовым ТУ для квартиры, ТУ заказчиком не переданы (К-4).

См. лист открытых вопросов (лист 6, записи К-1, К-2, К-4).

1000 мм · печать 1:1

| | | | | | | | | |
|---|---|---|---|---|---|---|---|---|
| | | | | | | **ГД-2026-008-АИ** | | |
| | | | | | | Квартира с кабинетом | | |
| | | | | | | Общая площадь 127,29* м² · * размеры со скана, не замерены (реестр — л. 6, К-1) | | |
| Изм. | Кол.уч | Лист | № док. | Подп. | Дата | | | |
| Разраб. | | Кырлан А.С. | | | 18.10.26 | Дизайн-проект интерьера | Стадия: РП | Лист: 13 / Листов: 92 |
| Пров. | | | | | | | | |
| ГИП | | | | | | | | |
| | | | | | | **План демонтажа и монтажа перегородок** | | |
| Н. контр. | | | | | | | | |
| Утв. | | | | | | М 1:100 | **Кырлан Александр Сергеевич** | |

выпуск 18.10.2026 № d2d5a25dca · стр. 16 из 129

# План дверей и ведомость заполнения проёмов

Проёмы, марки заполнения, привязки · размеры в мм

ПРЕДВАРИТЕЛЬНО · не для производства работ · открыто пунктов: 4 (реестр — л. 6)

**Допущения и предложения на листе**

Основа листа: размеры сняты с растрового плана заказчика с частичными размерами: рисунок не в масштабе, помещения выровнены по подписанным размерам мебели и проходов; контрольный обмер не выполнен (К-1); высота потолка 2700 мм принята: на плане заказчика её нет (К-2); толщины стен 300 / 120 мм приняты по плану заказчика, не замерены (К-1); разрешённая мощность 15 кВт принята по типовым ТУ для квартиры, ТУ заказчиком не переданы (К-4).

См. лист открытых вопросов (лист 6, записи К-1, К-2, К-4).

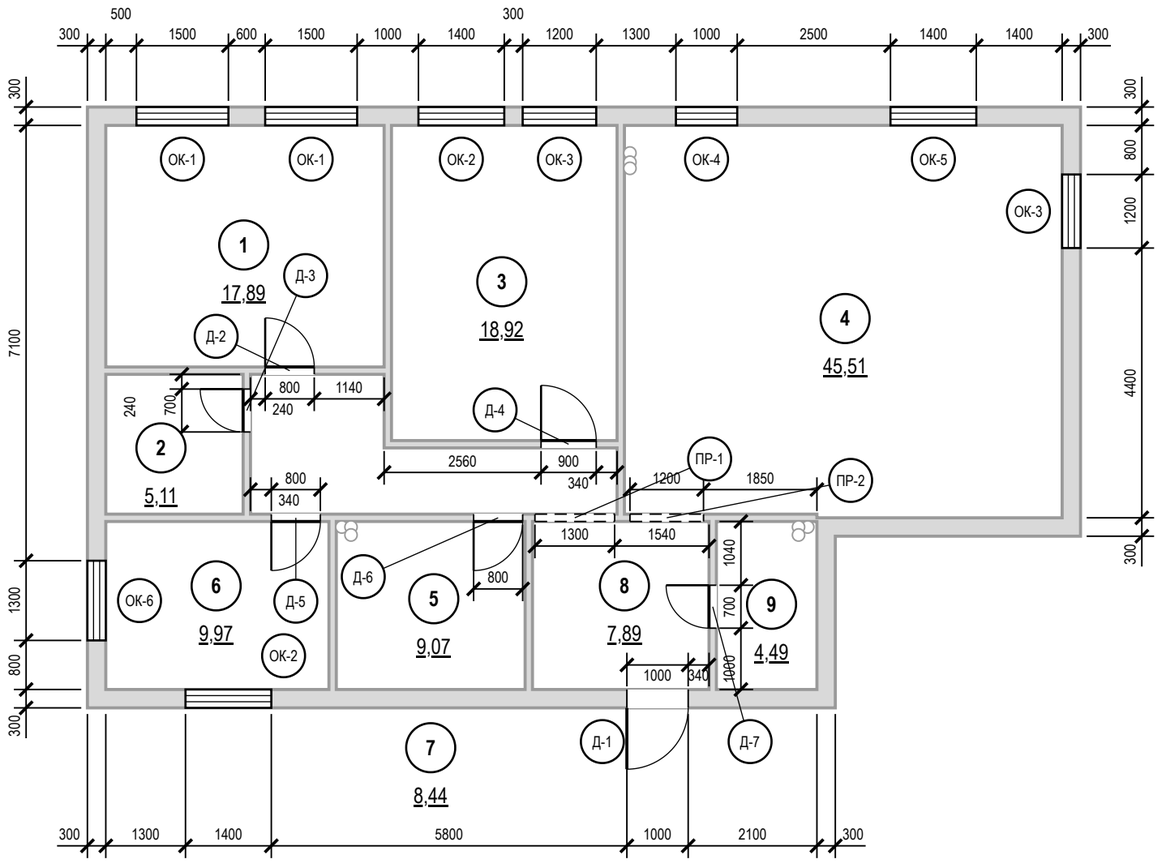


## Примечания

1. Размеры проёмов и привязки — в миллиметрах от чистых граней стен до отделки; привязка — от угла того помещения, со стороны которого стоит размер. Размер в ведомости — ширина × высота проёма от чистого пола 0,000. Откос от угла помещения до проёма с коробкой — не менее 50 мм.
2. Марки в кружках — типы заполнения проёмов (ГОСТ 21.501-2018, п. 5.3.2); одна марка — один типоразмер; количество сверено с планом.
3. Открывание: Л — петли слева, П — справа, если смотреть со стороны, куда открывается полотно (на себя).
4. Скрытые двери (Д-2…Д-7): проём замерить в чистоте; блок заказать до штукатурки (≈ 30 дн.), короб ставить до штукатурки; полотно навесить после чистовой отделки, красить в цвет стен. Порядок практика монтажа, изготовитель подтверждает.
5. Размер в ведомости — проёма: полотно скрытой двери уже проёма на коробку и зазор 10–15 мм (модель не выбрана); Д-2…Д-7 — существующие проёмы, до техзаключения не расширять.
6. Д-1: дуга наружу — по плану заказчика, не проверено; блок оставить или заменить — не решено.
7. Размеры проёмов и привязки сняты со скана плана заказчика и на объекте не замерены (обмерный план — лист 12).
8. Экспликация помещений — лист 12; в марках помещений — номер и площадь, м².
9. Привязка проёма к углу помещения меньше 1 мм на листе, размер на плане не показан: Д-6 — 40 мм; ПР-1 — 40 мм; ПР-2 — 90 мм.

1000 мм · печать 1:1

## Ведомость заполнения проёмов

| Марка | Наименование, обозначение | Проём ш×в, мм | Кол. | Откр. | Отделка полотна | Фурнитура | Прим. |
|---|---|---|---|---|---|---|---|
| Д-1 | Блок дверной входной, ГОСТ 31173-2016 | 1000×2100 | 1 | Л | в комплекте блока | в комплекте блока (замки, глазок) | наружу |
| Д-2 | Дверь скрытого монтажа, ТУ изготовителя | 800×2100 | 1 | П | окраска No. 15 с двух сторон | скрытые петли 3D, магнитный замок | |
| Д-3 | Дверь скрытого монтажа, ТУ изготовителя | 700×2100 | 1 | Л | V503 — пом. 2, No. 15 — пом. 5 | скрытые петли 3D, магнитный замок | |
| Д-4 | Дверь скрытого монтажа, ТУ изготовителя | 900×2100 | 1 | П | окраска No. 15 с двух сторон | скрытые петли 3D, магнитный замок | |
| Д-5 | Дверь скрытого монтажа, ТУ изготовителя | 800×2100 | 1 | Л | окраска No. 15 с двух сторон | скрытые петли 3D, магнитный замок | |
| Д-6 | Дверь скрытого монтажа, ТУ изготовителя | 800×2100 | 1 | Л | в тон облицовки — пом. 7, No. 15 — пом. 5 | скрытые петли 3D, магнитный замок, фиксатор WC | порог 15 |
| Д-7 | Дверь скрытого монтажа, ТУ изготовителя | 700×2100 | 1 | Л | No. 15 — пом. 8, в тон облицовки — пом. 9 | скрытые петли 3D, магнитный замок, фиксатор WC | порог 15 |
| ПР-1 | Портал без заполнения | 1300×2100 | 1 | | | | б/п |
| ПР-2 | Портал без заполнения | 1200×2100 | 1 | | | | б/п |
| ОК-1 | Блок оконный, ГОСТ 23166-2021 | 1500×1600 | 2 | | | | низ 800 |
| ОК-2 | Блок оконный, ГОСТ 23166-2021 | 1400×1600 | 2 | | | | низ 800 |
| ОК-3 | Блок оконный, ГОСТ 23166-2021 | 1200×1600 | 2 | | | | низ 800 |
| ОК-4 | Блок оконный, ГОСТ 23166-2021 | 1000×1400 | 1 | | | | низ 1000 |
| ОК-5 | Блок оконный, ГОСТ 23166-2021 | 1400×1600 | 1 | | | | низ 900 |
| ОК-6 | Блок оконный, ГОСТ 23166-2021 | 1300×1600 | 1 | | | | низ 800 |

## Условные обозначения

- стены (подложка обмера)
- дверь распашная, дуга открывания
- дверь скрытого монтажа
- дверь входная (полотно толще)
- портал (штрих — перемычка)
- оконный блок
- Д — марка типа (Д-N, ПР-N, ОК-N)
- 1 — номер помещения, площадь м²

| Изм. | Кол.уч | Лист | № док. | Подп. | Дата | ГД-2026-008-АИ | | | |
|---|---|---|---|---|---|---|---|---|---|
| | | | | | | Квартира с кабинетом | | | |
| | | | | | | Общая площадь 127,29* м² · * размеры со скана, не замерены (реестр — л. 6, К-1) | | | |
| Разраб. | | Кырлан А.С. | | | 18.10.26 | Дизайн-проект интерьера | Стадия | Лист | Листов |
| Пров. | | | | | | | РП | 14 | 92 |
| ГИП | | | | | | План дверей и ведомость заполнения проёмов | Кырлан Александр Сергеевич | | |
| Н. контр. | | | | | | М 1:100 | | | |
| Утв. | | | | | | | | | |

выпуск 18.10.2026 № d2d5a25dca · стр. 17 из 129

02

# Планировочное решение

Кырлан Александр Сергеевич

выпуск 18.10.2026 № d2d5a25dca · стр. 18 из 129

# Концепция интерьера

Модерн (ар-нуво) · схема аналоговая · 60/30/10 · материалы, образы и зонирование

## Идея

Стиль — модерн (ар-нуво): природность, плавность, камерность, ремесленность, поэтичность, приглушённая цветность, сумеречный тёплый свет. Модерн 60 % + современный (contemporary.json) 40 %. Стены — Bone No. 15 и льняной беж S 2010-Y30R, потолки — Winter V503, шалфей Calke Green No. 34 и пудровый Peignoir No. 286 вторым планом, акценты павлиний S 5030-B10G (бархат), горчица India Yellow No. 66, морёный дуб S 8010-Y30R; металл — латунь. Цветовая схема — аналоговая, пропорция 60/30/10: база на стенах и потолках, вторичный цвет — в текстиле и мягкой мебели, акцент — точечно.

## Мудборд: материалы и фактуры

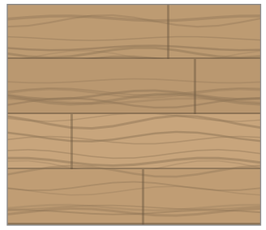

1167-4250
пол

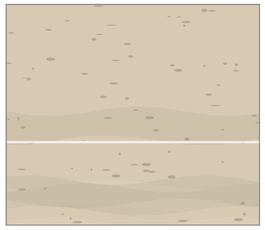

Керамогранит под травертин
фартук

 

Winter · Tikkurila V503
потолок, стены, плинтус

Bone — мягкий каменно-серый с зеленцой · Farrow & Ball No. 15
стены, плинтус

Calke Green — традиционный шалфей · Farrow & Ball No. 34
акцент (стена А)

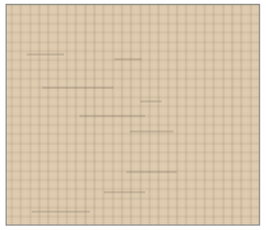

Лён, NCS S 2010-Y30R
портьеры-волна, подушки декоративные на кровать

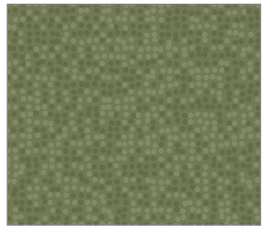

Шерсть, NCS S 5020-G50Y
ковёр под кроватью

Бархат, Farrow & Ball No. 34
подушки на кровать, подушки на диван

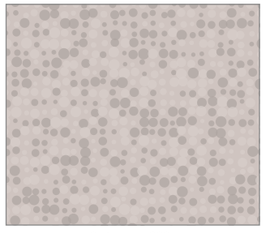

Букле, Farrow & Ball No. 286
подушки декоративные на кровать

## Палитра 60/30/10

60 % база — Farrow & Ball No. 15 Bone — мягкий каменно-серый с зеленцой, LRV 53; NCS S 2010-Y30R Тёплый льняной беж, LRV 60; Tikkurila V503 Winter, LRV 86

30 % вторичный — Farrow & Ball No. 34 Calke Green — традиционный шалфей, LRV 22; Farrow & Ball No. 286 Peignoir серо-розовый, LRV 57

10 % акцент — NCS S 5030-B10G Павлиний сине-зелёный, LRV 12; Farrow & Ball No. 66 India Yellow — глубокая горчица, LRV 36; NCS S 8010-Y30R Тёмно-коричневый, LRV 3

## Функциональное зонирование (М 1:200)

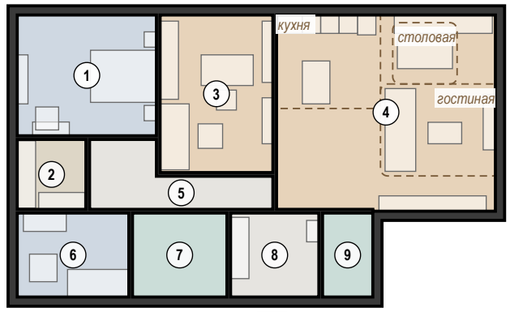


- дневная зона: гостиная, кухня, столовая
- ночная зона: спальни
- мокрая зона: санузлы
- хранение: гардеробная, кладовая
- вход и коммуникации
- функциональная зона в помещении
- (1) номер помещения (лист 16)

## Образы помещений

**4. Кухня-гостиная** — 45,51 м²
стены Farrow & Ball No. 15; акцент No. 34 на стене А
пол — 1167-4250

**1. Спальня** — 17,89 м²
стены Farrow & Ball No. 15; акцент No. 34 на стене А
пол — 1167-4250

**6. Детская** — 9,97 м²
стены Farrow & Ball No. 15; акцент No. 34 на стене А
пол — 1167-4250

**3. Кабинет** — 18,92 м²
стены Farrow & Ball No. 15; акцент No. 34 на стене А
пол — 1167-4250

**8. Прихожая** — 7,89 м²
стены Farrow & Ball No. 15
пол — A8UZ
декор: зеркало

**5. Коридор** — 9,07 м²
стены Farrow & Ball No. 15
пол — 1167-4250
свет 3000 K

**2. Гардеробная-постирочная** — 5,11 м²
стены Tikkurila V503
пол — 1167-4250
свет 3000 K

**7. Ванная** — 8,44 м²
стены Atlas Concorde A8UZ
пол — A8UZ
свет 3000 K

**9. Санузел гостевой** — 4,49 м²
стены Atlas Concorde A8UZ
пол — A8UZ
свет 3000 K

## Материалы и отделка

**1167-4250**
пол — пом. 1, 2, 3, 4, 5, 6

**Керамогранит под травертин**
матовый; 1200×600
фартук — пом. 4

**A8UZ**
пол, стены — пом. 7, 8, 9

**Farrow & Ball No. 15 Bone — мягкий каменно-серый с зеленцой, LRV 53**
Farrow & Ball Modern Emulsion, матовая
стены, плинтус — пом. 1, 3, 4, 5, 6, 8

**Tikkurila V503 Winter, LRV 86**
Tikkurila Anti-Reflex 2, глубокоматовая
потолок, стены, плинтус — пом. 1, 2, 3, 4, 5, 6, 7, 8, 9

**Farrow & Ball No. 34 Calke Green — традиционный шалфей, LRV 22**
акцентная стена
акцент (стена А) — пом. 1, 3, 4, 6

## Текстиль и металл

**Лён, NCS S 2010-Y30R**
портьеры-волна, подушки декоративные на кровать

**Шерсть, NCS S 5020-G50Y**
ковёр под кроватью

**Шерсть, Farrow & Ball No. 34**
плед на кровать

**Букле, Farrow & Ball No. 286**
подушки декоративные на кровать

**Чёрный матовый металл**
зеркало в рост, зеркало

**Вуаль, Tikkurila V503**
тюль

**Бархат, Farrow & Ball No. 34**
подушки на кровать, подушки на диван

**Шерсть, Farrow & Ball No. 66**
ковёр под кроватью, ковёр в зоне отдыха

**Бархат, NCS S 5030-B10G**
подушки на кровать

**Лён, Farrow & Ball No. 66**
римская штора

## Чего избегаем

1) Пластиковая волна: гнутые МДФ-фасады и ПВХ-лепнина без пропорций выглядят пародией
2) Смешивать с ар-деко (острая геометрия, хром, чёрный глянец — другой стиль)
3) Холодные белые стены и хром: модерн живёт в приглушённых тёплых тонах и патинированном металле
4) Яркие кислотные зелёные и чистый фиолетовый — нужны землистые, приглушённые
5) Перегрузка: растительный орнамент одновременно на обоях, шторах, ковре и мебели — выбрать одного солиста
6) Витражная плёнка-самоклейка вместо стекла

**Допущения и предложения на листе**

Основа листа: размеры сняты с растрового плана заказчика с частичными размерами: рисунок не в масштабе, помещения выровнены по подписанным размерам мебели и проходов; контрольный обмер не выполнен (К-1); высота потолка 2700 мм принята: на плане заказчика её нет (К-2); толщины стен 300 / 120 мм приняты по плану заказчика, не замерены (К-1); разрешённая мощность 15 кВт принята по типовым ТУ для квартиры, ТУ заказчиком не переданы (К-4).
См. лист открытых вопросов (лист 6, записи К-1, К-2, К-4).

## Примечания

1. Коды цвета — по веерам производителей (колерная карта, лист 42); перед закупкой краски — выкрас на стене объекта под дневным светом и лампами проекта.
2. Материалы — по ведомости отделки (лист 40); мебель, текстиль и декор — по спецификации (лист 17). Образцы доски, керамогранита и тканей утвердить до заказа.
3. Фактуры на листе условные, цвет передан по HEX-значениям производителей: при печати возможны отклонения, решение — только по физическому образцу.

| Изм. | Кол.уч | Лист | № док. | Подп. | Дата |
|---|---|---|---|---|---|
| Разраб. | | Кырлан А.С. | | | 18.10.26 |
| Пров. | | | | | |
| ГИП | | | | | |
| Н. контр. | | | | | |
| Утв. | | | | | |

**ГД-2026-008-АИ**

Квартира с кабинетом

Общая площадь 127,29* м² · * размеры со скана, не замерены (реестр — л. 6, К-1)

Дизайн-проект интерьера

| Стадия | Лист | Листов |
|---|---|---|
| РП | 15 | 92 |

**Концепция интерьера**
М б/м

**Кырлан Александр Сергеевич**

выпуск 18.10.2026 № d2d5a25dca · стр. 19 из 129

# План расстановки мебели

Мебель и оборудование · размеры в мм от чистовых стен · марки — по ведомости

ПРЕДВАРИТЕЛЬНО · не для производства работ · открыто пунктов: 4 (реестр — л. 6)

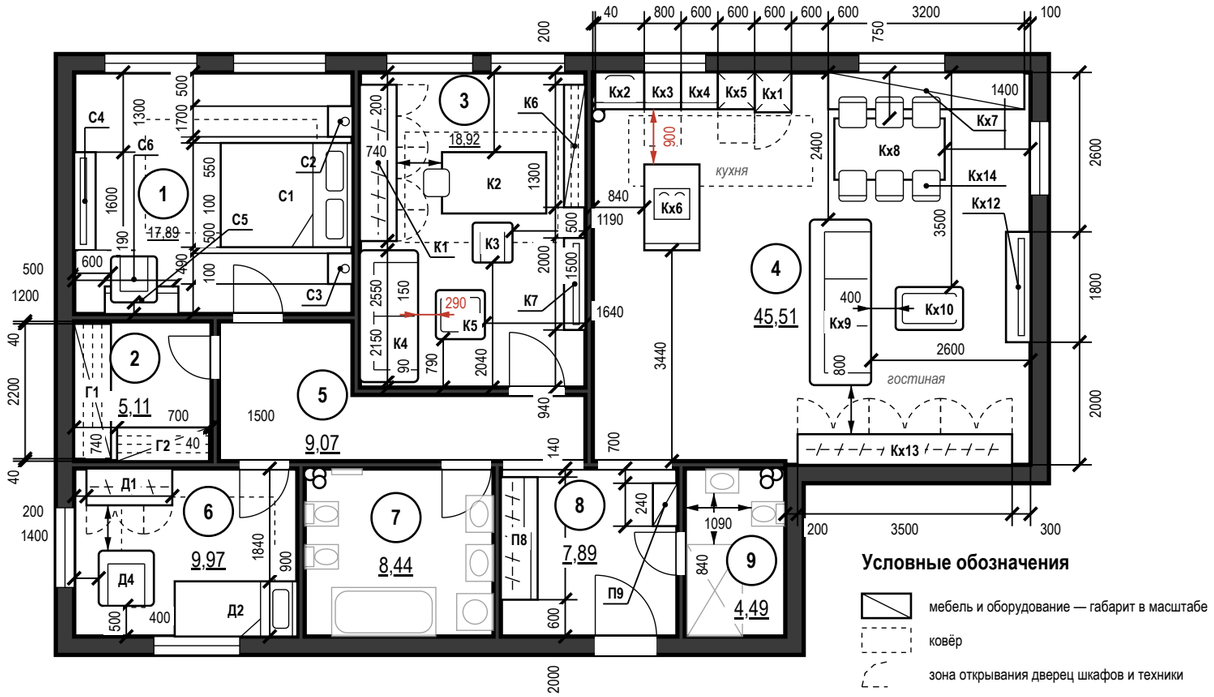


## Условные обозначения

- мебель и оборудование — габарит в масштабе
- ковёр
- зона открывания дверец шкафов и техники
- К1 — марка предмета по ведомости мебели
- привязка от чистовой стены, мм
- ширина прохода, зазор, мм
- проход меньше нормы — расстановку изменить
- сантехприборы — подложка (лист ВК)
- существующие стены (сечение)
- стояк: К1 — канализация, В1 — ХВС, Т3 — ГВС
- 1 — номер помещения, площадь м²
- *зона* — функциональная зона помещения

**Экспликация помещений**

лист 12 · на плане — номера в марках

## Ведомость мебели и оборудования

| Марка | Наименование | Ш×Г×В, мм | Пом. | Кол. |
|---|---|---|---|---|
| С1 | Кровать 1700×2150 с высоким | 1700×2150×450 | 1 | 1 |
| С2 | Тумба прикроватная | 500×400×550 | 1 | 1 |
| С3 | Тумба прикроватная | 500×400×550 | 1 | 1 |
| С4 | ТВ на стене | 1600×350×450 | 1 | 1 |
| С5 | Туалетный столик с овальным | 1200×450×780 | 1 | 1 |
| С6 | Кресло-ракушка | 750×750×800 | 1 | 1 |
| Г1 | Система хранения | 2200×600×2400 | 2 | 1 |
| Г2 | Шкаф с выдвижной гладильной | 1500×550×2400 | 2 | 1 |
| К1 | Шкаф распашной с арочными фасадами | 2550×600×2400 | 3 | 1 |
| К2 | Рабочий стол 1700×1000 | 1000×1700×750 | 3 | 1 |
| К3 | Кресло рабочее | 650×650×900 | 3 | 1 |
| К4 | Диван 2150 с мягкими | 2150×950×800 | 3 | 1 |
| К5 | Столик кофейный круглый | 800×800×420 | 3 | 1 |
| К6 | Стеллаж-библиотека с арками | 2000×350×2400 | 3 | 1 |
| К7 | ТВ на стене | 1500×350×450 | 3 | 1 |
| Кх1 | Колонна с холодильником | 600×650×2100 | 4 | 1 |
| Кх2 | Модуль под мойку у окна | 800×600×900 | 4 | 1 |
| Кх3 | Посудомоечная машина встроенная | 600×600×900 | 4 | 1 |
| Кх4 | Модуль с ящиками | 600×600×900 | 4 | 1 |
| Кх5 | Колонна | 600×600×2100 | 4 | 1 |
| Кх6 | Остров 900×1400 с варочной панелью | 900×1400×900 | 4 | 1 |
| Кх7 | Банкетка-диван вдоль окон | 3200×600×850 | 4 | 1 |
| Кх8 | Стол обеденный овальный 1800×1000 | 1800×1000×750 | 4 | 1 |
| Кх9 | Диван угловой модульный с | 2700×1000×800 | 4 | 1 |
| Кх10 | Столик журнальный органической формы | 1100×700×380 | 4 | 1 |
| Кх12 | ТВ-стена с биокамином | 1800×400×500 | 4 | 1 |
| Кх13 | Шкаф встроенный | 3500×500×2400 | 4 | 1 |
| Д1 | Шкаф с арочной нишей | 1400×600×2400 | 6 | 1 |
| Д2 | Кровать 900×2000 с мягким | 900×2000×450 | 6 | 1 |
| Д4 | Подвесное кресло-кокон | 900×900×1100 | 6 | 1 |
| П8 | Шкаф-купе с зеркальными арками | 2000×600×2600 | 8 | 1 |
| П9 | Пуф и вешалка | 700×400×450 | 8 | 1 |
| Кх14 | Стул обеденный к столу Кх8 | 450×500×820 | 4 | 6 |

Ш — вдоль стены (изголовья), Г — от стены (длина кровати)

Материалы, модели, допуск замены — лист 17

## Примечания

1. Размеры даны в мм от чистовых поверхностей стен: слой штукатурки 20 мм по блоку и 5 мм шпаклёвки по ГКЛ учтён. Перед заказом встроенной мебели контрольный обмер после штукатурки.
2. Привязки мебели — от стен и углов помещения, а не от другой мебели; ширина проходов и зазоров показана стрелками.
3. Розетки, выводы и выключатели под мебель — см. лист 20 «План розеток и электровыводов»; сантехприборы и выводы воды — лист 30.
4. План расстановки не является документацией для изготовления мебели: изделия — по чертежам мебельщика; покупную мебель заменять только на изделия не больше габарита из спецификации (лист 17).
5. Встроенная мебель «стена в стену» — с зазором 10 мм с каждой стороны или с компенсаторами.
6. Стулья обеденной группы (Кх14 — 6 шт.) показаны в рабочем положении, задвинутыми под столешницу на 150 мм.

**Допущения и предложения на листе**

Основа листа: размеры сняты с растрового плана заказчика с частичными размерами: рисунок не в масштабе, помещения выровнены по подписанным размерам мебели и проходов; контрольный обмер не выполнен (К-1); высота потолка 2700 мм принята: на плане заказчика её нет (К-2); толщины стен 300 / 120 мм приняты по плану заказчика, не замерены (К-1); разрешённая мощность 15 кВт принята по типовым ТУ для квартиры, ТУ заказчиком не переданы (К-4).

Открытые вопросы и конфликты по листу: К-1.

См. лист открытых вопросов (лист 6, записи К-1, К-2, К-4).

1000 мм · печать 1:1

| Изм. | Кол.уч | Лист | № док. | Подп. | Дата |
|---|---|---|---|---|---|
| Разраб. | | Кырлан А.С. | | | 18.10.26 |
| Пров. | | | | | |
| ГИП | | | | | |
| Н. контр. | | | | | |
| Утв. | | | | | |

**ГД-2026-008-АИ**

Квартира с кабинетом

Общая площадь 127,29* м² · * размеры со скана, не замерены (реестр — л. 6, К-1)

Дизайн-проект интерьера

| Стадия | Лист | Листов |
|---|---|---|
| РП | 16 | 92 |

**План расстановки мебели**

М 1:100

**Кырлан Александр Сергеевич**

выпуск 18.10.2026 № d2d5a25dca · стр. 20 из 129

# Спецификация мебели и оборудования

**ПРЕДВАРИТЕЛЬНО · не для производства работ · открыто пунктов: 4 (реестр — л. 6)**

Форма 1 ГОСТ 21.110-2013 · позиции мебели — по плану расстановки

| Поз. | Наименование и техническая характеристика | Тип, марка, обозначение документа, опросного листа | Код продукции | Поставщик | Ед. измерения | Кол. | Масса 1 ед., кг | Примечание |
|---|---|---|---|---|---|---|---|---|
| | **Мебель встроенная и корпусная (изготовление по чертежам мебельщика)** | | | | | | | |
| Г1 | Система хранения: штанги, полки, ящики; каркас и полки — ЛДСП, декор «дуб натуральный»; Ш×Г×В 2200×600×2400 мм | | | изготовление на заказ | шт. | 1 | | пом. 2; крепление к стене |
| Г2 | Шкаф с выдвижной гладильной доской и полками; каркас и полки — ЛДСП, декор «дуб натуральный»; Ш×Г×В 1500×550×2400 мм | | | изготовление на заказ | шт. | 1 | | пом. 2; крепление к стене |
| К1 | Шкаф распашной с арочными фасадами; корпус ЛДСП, фасады — матовая эмаль в цвет стен (Farrow & Ball No. 15); Ш×Г×В 2550×600×2400 мм | | | изготовление на заказ | шт. | 1 | | пом. 3 |
| Кх1 | Колонна с холодильником; корпус ЛДСП, фасады — матовая эмаль в тон стен; Ш×Г×В 600×650×2100 мм | | | изготовление на заказ | шт. | 1 | | пом. 4 |
| Кх2 | Модуль под мойку у окна; корпус ЛДСП, фасады — матовая эмаль в тон стен; Ш×Г×В 800×600×900 мм | | | изготовление на заказ | шт. | 1 | | пом. 4 |
| Кх3 | Посудомоечная машина встроенная; корпус ЛДСП, фасады — матовая эмаль в тон стен; Ш×Г×В 600×600×900 мм | | | изготовление на заказ | шт. | 1 | | пом. 4 |
| Кх4 | Модуль с ящиками; корпус ЛДСП, фасады — матовая эмаль в тон стен; Ш×Г×В 600×600×900 мм | | | изготовление на заказ | шт. | 1 | | пом. 4 |
| Кх5 | Колонна: духовой шкаф и СВЧ; корпус ЛДСП, фасады — матовая эмаль в тон стен; Ш×Г×В 600×600×2100 мм | | | изготовление на заказ | шт. | 1 | | пом. 4 |
| Кх6 | Остров 900×1400 с варочной панелью, столешница — травертин; корпус ЛДСП, фасады — матовая эмаль в тон стен; Ш×Г×В 900×1400×900 мм | | | изготовление на заказ | шт. | 1 | | пом. 4 |
| Кх13 | Шкаф встроенный, фасады с округлыми торцами; корпус ЛДСП, фасады — матовая эмаль в цвет стен (Farrow & Ball No. 15); Ш×Г×В 3500×500×2400 мм | | | изготовление на заказ | шт. | 1 | | пом. 4 |
| Д1 | Шкаф с арочной нишей; корпус ЛДСП, фасады — матовая эмаль в цвет стен (Farrow & Ball No. 15); Ш×Г×В 1400×600×2400 мм | | | изготовление на заказ | шт. | 1 | | пом. 6; крепление к стене |
| П8 | Шкаф-купе с зеркальными арками; корпус ЛДСП, фасады — матовая эмаль в цвет стен (Farrow & Ball No. 15); Ш×Г×В 2000×600×2600 мм | | | изготовление на заказ | шт. | 1 | | пом. 8 |
| | **Мебель покупная** | | | | | | | |
| С1 | Кровать 1700×2150 с высоким округлым изголовьем, бархат; мягкое изголовье, обивка — ткань, цвет Farrow & Ball No. 34; Ш×Г×В 1700×2150×450 мм | | | аналог по характеристикам | шт. | 1 | | пом. 1; замена ≤ габарита |
| С2, С3 | Тумба прикроватная, морёный дуб, латунные ручки; шпон, дуб натуральный, матовое масло; Ш×Г×В 500×400×550 мм | | | аналог по характеристикам | шт. | 2 | | пом. 1; замена ≤ габарита |
| С4 | ТВ на стене, тумба подвесная с волнистым фасадом; шпон, дуб натуральный, матовое масло; Ш×Г×В 1600×350×450 мм | | | аналог по характеристикам | шт. | 1 | | пом. 1; замена ≤ габарита |
| С5 | Туалетный столик с овальным зеркалом в латунной раме; шпон, дуб натуральный, матовое масло; Ш×Г×В 1200×450×780 мм | | | аналог по характеристикам | шт. | 1 | | пом. 1; замена ≤ габарита |
| С6 | Кресло-ракушка, бархат павлиньего цвета; обивка — ткань, цвет Farrow & Ball No. 34; Ш×Г×В 750×750×800 мм | | | аналог по характеристикам | шт. | 1 | | пом. 1; замена ≤ габарита |
| К2 | Рабочий стол 1700×1000, морёный дуб, округлые углы; шпон, дуб натуральный, матовое масло; Ш×Г×В 1000×1700×750 мм | | | аналог по характеристикам | шт. | 1 | | пом. 3; замена ≤ габарита |
| К3 | Кресло рабочее, кожа карамельного цвета; обивка — ткань, цвет Farrow & Ball No. 34; Ш×Г×В 650×650×900 мм | | | аналог по характеристикам | шт. | 1 | | пом. 3; замена ≤ габарита |
| К4 | Диван 2150 с мягкими округлыми подлокотниками; обивка — ткань, цвет Farrow & Ball No. 34; Ш×Г×В 2150×950×800 мм | | | аналог по характеристикам | шт. | 1 | | пом. 3; замена ≤ габарита |
| К5 | Столик кофейный круглый, травертин; шпон, дуб натуральный, матовое масло; Ш×Г×В 800×800×420 мм | | | аналог по характеристикам | шт. | 1 | | пом. 3; замена ≤ габарита |
| К6 | Стеллаж-библиотека с арками; шпон, дуб натуральный, матовое масло; Ш×Г×В 2000×350×2400 мм | | | аналог по характеристикам | шт. | 1 | | пом. 3; замена ≤ габарита |
| К7 | ТВ на стене, тумба подвесная; шпон, дуб натуральный, матовое масло; Ш×Г×В 1500×350×450 мм | | | аналог по характеристикам | шт. | 1 | | пом. 3; замена ≤ габарита |
| Кх7 | Банкетка-диван вдоль окон, бархат; Ш×Г×В 3200×600×850 мм | | | аналог по характеристикам | шт. | 1 | | пом. 4; замена ≤ габарита |
| Кх8 | Стол обеденный овальный 1800×1000, морёный дуб; шпон, дуб натуральный, матовое масло; Ш×Г×В 1800×1000×750 мм | | | аналог по характеристикам | шт. | 1 | | пом. 4; замена ≤ габарита |

## Примечания

1. Позиции мебели совпадают с марками на плане расстановки (лист 16); размеры Ш×Г×В — Ш вдоль стены, Г от стены.
2. Встроенная и корпусная мебель изготавливается по чертежам мебельщика после контрольного обмера; графы «Тип, марка» и «Код продукции» для неё не заполняются (ГОСТ 21.110-2013).
3. Покупные изделия — аналог по характеристикам: заменять только на изделия не больше указанного габарита и того же материала и цвета.
4. Материал и цвет, не указанные в данных изделия, приняты по концепции (лист 15): тон дерева — по полу, обивка — по вторичному цвету палитры; образцы согласовать до заказа.
5. Масса 1 ед. для изделий до 25 кг не указывается. Техника — по монтажным схемам изготовителя; выводы — по листам ЭОМ и ВК.

**Допущения и предложения на листе**

Основа листа: размеры сняты с растрового плана заказчика с частичными размерами: рисунок не в масштабе, помещения выровнены по подписанным размерам мебели и проходов; контрольный обмер не выполнен (К-1); высота потолка 2700 мм принята: на плане заказчика её нет (К-2); толщины стен 300 / 120 мм приняты по плану заказчика, не замерены (К-1); разрешённая мощность 15 кВт принята по типовым ТУ для квартиры, ТУ заказчиком не переданы (К-4).
См. лист открытых вопросов (лист 6, записи К-1, К-2, К-4).

| Изм. | Кол.уч | Лист | № док. | Подп. | Дата |
|---|---|---|---|---|---|
| Разраб. | | Кырлан А.С. | | | 18.10.26 |
| Пров. | | | | | |
| ГИП | | | | | |
| | | | | | |
| Н. контр. | | | | | |
| Утв. | | | | | |

**ГД-2026-008-АИ**

Квартира с кабинетом

Общая площадь 127,29* м² · * размеры со скана, не замерены (реестр — л. 6, К-1)

Дизайн-проект интерьера

| Стадия | Лист | Листов |
|---|---|---|
| РП | 17 | 92 |

**Спецификация мебели и оборудования**

М б/м

**Кырлан Александр Сергеевич**

выпуск 18.10.2026 № d2d5a25dca · стр. 21 из 129

# Спецификация мебели и оборудования (продолжение)

Форма 1 ГОСТ 21.110-2013 · позиции мебели — по плану расстановки

**ПРЕДВАРИТЕЛЬНО · не для производства работ · открыто пунктов: 4 (реестр — л. 6)**

| Поз. | Наименование и техническая характеристика | Тип, марка, обозначение документа, опросного листа | Код продукции | Поставщик | Ед. измерения | Кол. | Масса 1 ед., кг | Примечание |
|---|---|---|---|---|---|---|---|---|
| Кх9 | Диван угловой модульный с округлыми формами, бархат павлиньего цвета; обивка — ткань, цвет Farrow & Ball No. 34; Ш×Г×В 2700×1000×800 мм | | | аналог по характеристикам | шт. | 1 | | пом. 4; замена ≤ габарита |
| Кх10 | Столик журнальный органической формы, травертин; шпон, дуб натуральный, матовое масло; Ш×Г×В 1100×700×380 мм | | | аналог по характеристикам | шт. | 1 | | пом. 4; замена ≤ габарита |
| Кх12 | ТВ-стена с биокамином, панели с волнистым рельефом; шпон, дуб натуральный, матовое масло; Ш×Г×В 1800×400×500 мм | | | аналог по характеристикам | шт. | 1 | | пом. 4; замена ≤ габарита |
| Кх14 | Стул обеденный к столу Кх8; обивка — ткань, цвет Farrow & Ball No. 34; каркас — дуб натуральный; Ш×Г×В 450×500×820 мм | | | аналог по характеристикам | шт. | 6 | | пом. 4; замена ≤ габарита |
| Д2 | Кровать 900×2000 с мягким изголовьем-облаком; мягкое изголовье, обивка — ткань, цвет Farrow & Ball No. 34; Ш×Г×В 900×2000×450 мм | | | аналог по характеристикам | шт. | 1 | | пом. 6; замена ≤ габарита |
| Д4 | Подвесное кресло-кокон; обивка — ткань, цвет Farrow & Ball No. 34; Ш×Г×В 900×900×1100 мм | | | аналог по характеристикам | шт. | 1 | | пом. 6; замена ≤ габарита |
| П9 | Пуф и вешалка; Ш×Г×В 700×400×450 мм | | | аналог по характеристикам | шт. | 1 | | пом. 8; замена ≤ габарита |
| | **Техника встраиваемая и бытовая, светильники под розетки** | | | | | | | |
| | Холодильник встраиваемый, в модуле Кх1 | | | аналог по характеристикам | шт. | 1 | | пом. 4; по схеме изготовителя |
| | Посудомоечная машина встраиваемая, в модуле Кх3; ниша 600 мм | | | аналог по характеристикам | шт. | 1 | | пом. 4; по схеме изготовителя |
| | Духовой шкаф встраиваемый, в модуле Кх5 | | | аналог по характеристикам | шт. | 1 | | пом. 4; по схеме изготовителя |
| | СВЧ-печь встраиваемая, в модуле Кх5 | | | аналог по характеристикам | шт. | 1 | | пом. 4; по схеме изготовителя |
| | Варочная панель встраиваемая, электрическая, в модуле Кх6 | | | аналог по характеристикам | шт. | 1 | | пом. 4; по схеме изготовителя |
| | Вытяжка, у Кх13 | | | аналог по характеристикам | шт. | 1 | | пом. 4; вывод ЭВ3 (ЭОМ) |
| | Стиральная машина, место по листу ВК (П6); Ш×Г 600×600 мм | | | аналог по характеристикам | шт. | 1 | | пом. 7; по схеме изготовителя |
| | Торшер, у поз. С4; абажур — ткань или опаловое стекло; лампа 2700 K | | | аналог по характеристикам | шт. | 1 | | пом. 1; розетка Р5 (ЭОМ) |
| | Торшер, у поз. Кх2; абажур — ткань или опаловое стекло; лампа 2700 K | | | аналог по характеристикам | шт. | 1 | | пом. 4; розетка Р21 (ЭОМ) |
| | **Текстиль** | | | | | | | |
| Т1 | Портьеры-волна; лён 100 %; цвет NCS S 2010-Y30R; карниз 2500 мм, высота 2610 мм, сборка 2 | | | аналог по характеристикам | шт. | 2 | | пом. 1 |
| Т2 | Тюль; полиэстер 100 %; цвет Tikkurila V503; карниз 2500 мм, высота 2610 мм, сборка 2,5 | | | аналог по характеристикам | шт. | 1 | | пом. 1 |
| Т3 | Ковёр под кроватью; шерсть 80 %, хлопок 20 %; цвет NCS S 5020-G50Y; 2800×1850 мм | | | аналог по характеристикам | шт. | 1 | | пом. 1; с подложкой |
| Т4 | Подушки декоративные на кровать; лён 100 %; цвет NCS S 2010-Y30R | | | аналог по характеристикам | шт. | 3 | | пом. 1 |
| Т5 | Подушки на кровать, акцент; хлопковый бархат 100 %; цвет Farrow & Ball No. 34 | | | аналог по характеристикам | шт. | 2 | | пом. 1 |
| Т6 | Плед на кровать; шерсть мериноса 100 %; цвет Farrow & Ball No. 34 | | | аналог по характеристикам | шт. | 1 | | пом. 1 |
| Т7 | Портьеры-волна; лён 100 %; цвет NCS S 2010-Y30R; карниз 1820 мм, высота 2610 мм, сборка 2 | | | аналог по характеристикам | шт. | 2 | | пом. 3 |
| Т8 | Тюль; полиэстер 100 %; цвет Tikkurila V503; карниз 1820 мм, высота 2610 мм, сборка 2,5 | | | аналог по характеристикам | шт. | 1 | | пом. 3 |
| Т9 | Ковёр под кроватью; шерсть 100 %; цвет Farrow & Ball No. 66; 2500×1800 мм | | | аналог по характеристикам | шт. | 1 | | пом. 3; с подложкой |
| Т10 | Подушки декоративные на кровать; букле (шерсть 60 %, полиэстер 40 %); цвет Farrow & Ball No. 286 | | | аналог по характеристикам | шт. | 3 | | пом. 3 |

**Допущения и предложения на листе**

Основа листа: размеры сняты с растрового плана заказчика с частичными размерами: рисунок не в масштабе, помещения выровнены по подписанным размерам мебели и проходов; контрольный обмер не выполнен (К-1); высота потолка 2700 мм принята: на плане заказчика её нет (К-2); толщины стен 300 / 120 мм приняты по плану заказчика, не замерены (К-1); разрешённая мощность 15 кВт принята по типовым ТУ для квартиры, ТУ заказчиком не переданы (К-4).

См. лист открытых вопросов (лист 6, записи К-1, К-2, К-4).

| Изм. | Кол.уч | Лист | № док. | Подп. | Дата |
|---|---|---|---|---|---|
| Разраб. | | Кырлан А.С. | | | 18.10.26 |
| Пров. | | | | | |
| ГИП | | | | | |
| | | | | | |
| Н. контр. | | | | | |
| Утв. | | | | | |

**ГД-2026-008-АИ**

Квартира с кабинетом

Общая площадь 127,29* м² · * размеры со скана, не замерены (реестр — л. 6, К-1)

| Дизайн-проект интерьера | Стадия | Лист | Листов |
|---|---|---|---|
| | РП | 18 | 92 |

**Спецификация мебели и оборудования (продолжение)**
М б/м

**Кырлан Александр Сергеевич**

# Спецификация мебели и оборудования (продолжение)

Форма 1 ГОСТ 21.110-2013 · позиции мебели — по плану расстановки

**ПРЕДВАРИТЕЛЬНО · не для производства работ · открыто пунктов: 4 (реестр — л. 6)**

| Поз. | Наименование и техническая характеристика | Тип, марка, обозначение документа, опросного листа | Код продукции | Поставщик | Ед. измерения | Кол. | Масса 1 ед., кг | Примечание |
|---|---|---|---|---|---|---|---|---|
| Т11 | Подушки на кровать, акцент; хлопковый бархат 100 %; цвет NCS S 5030-B10G | | | аналог по характеристикам | шт. | 2 | | пом. 3 |
| Т12 | Плед на кровать; шерсть мериноса 100 %; цвет Farrow & Ball No. 34 | | | аналог по характеристикам | шт. | 1 | | пом. 3 |
| Т13 | Портьеры-волна (гостиная); лён 70 %, вискоза 30 %; цвет NCS S 2010-Y30R; карниз 2250 мм, высота 2610 мм, сборка 2 | | | аналог по характеристикам | шт. | 2 | | пом. 4 |
| Т14 | Тюль (гостиная); полиэстер 100 %; цвет Tikkurila V503; карниз 2250 мм, высота 2610 мм, сборка 2,5 | | | аналог по характеристикам | шт. | 1 | | пом. 4 |
| Т15 | Римская штора (кухня); лён 100 %; цвет Farrow & Ball No. 66; карниз 1400 мм, высота 1620 мм | | | аналог по характеристикам | шт. | 1 | | пом. 4 |
| Т16 | Ковёр в зоне отдыха; шерсть 100 %; цвет Farrow & Ball No. 66; 3000×1150 мм | | | аналог по характеристикам | шт. | 1 | | пом. 4; с подложкой |
| Т17 | Подушки на диван; букле (шерсть 60 %, полиэстер 40 %); цвет NCS S 2010-Y30R | | | аналог по характеристикам | шт. | 3 | | пом. 4 |
| Т18 | Подушки на диван, акцент; хлопковый бархат 100 %; цвет Farrow & Ball No. 34 | | | аналог по характеристикам | шт. | 2 | | пом. 4 |
| Т19 | Плед на диван; альпака 50 %, шерсть 50 %; цвет Farrow & Ball No. 66 | | | аналог по характеристикам | шт. | 1 | | пом. 4 |
| Т20 | Портьеры-волна; лён 100 %; цвет NCS S 2010-Y30R; карниз 1820 мм, высота 2610 мм, сборка 2 | | | аналог по характеристикам | шт. | 2 | | пом. 6 |
| Т21 | Тюль; полиэстер 100 %; цвет Tikkurila V503; карниз 1820 мм, высота 2610 мм, сборка 2,5 | | | аналог по характеристикам | шт. | 1 | | пом. 6 |
| Т22 | Ковёр под кроватью; шерсть 100 %; цвет Farrow & Ball No. 66; 2500×1800 мм | | | аналог по характеристикам | шт. | 1 | | пом. 6; с подложкой |
| Т23 | Подушки декоративные на кровать; букле (шерсть 60 %, полиэстер 40 %); цвет Farrow & Ball No. 286 | | | аналог по характеристикам | шт. | 3 | | пом. 6 |
| Т24 | Подушки на кровать, акцент; хлопковый бархат 100 %; цвет NCS S 5030-B10G | | | аналог по характеристикам | шт. | 2 | | пом. 6 |
| Т25 | Плед на кровать; шерсть мериноса 100 %; цвет Farrow & Ball No. 34 | | | аналог по характеристикам | шт. | 1 | | пом. 6 |
| | **Декор** | | | | | | | |
| ДК1 | Картина над кроватью: абстракция, холст, тонкая рама из дуба; 1200×700 мм; низ на 1300 мм от пола | | | аналог по характеристикам | шт. | 1 | 4 | пом. 1; крепление к стене |
| ДК3 | Картина над диваном: графика в паспарту, рама — дуб; 1400×700 мм; низ на 1000 мм от пола | | | аналог по характеристикам | шт. | 1 | 4 | пом. 3; крепление к стене |
| ДК4 | Зеркало в рост в тонкой чёрной раме; рама — чёрный матовый; 600×1600 мм; низ на 300 мм от пола | | | аналог по характеристикам | шт. | 1 | 12 | пом. 3; крепление: анкер для пустотелых оснований, 4 шт. |
| ДК6 | Картина: крупная абстракция в тёплой гамме, холст на подрамнике; 1200×900 мм; центр на 1550 мм от пола | | | аналог по характеристикам | шт. | 1 | 6 | пом. 4; крепление: анкер, 2 шт. |
| ДК7 | Растение в кашпо; 450×450 мм | | | аналог по характеристикам | шт. | 1 | | пом. 4 |
| ДК8 | Ваза керамическая с ветками на обеденном столе; 200×350 мм; на М5 | | | аналог по характеристикам | шт. | 1 | | пом. 4 |
| ДК2 | Картина над кроватью: графика в паспарту, рама — дуб; 600×700 мм; низ на 1100 мм от пола | | | аналог по характеристикам | шт. | 1 | 4 | пом. 6; крепление к стене |
| ДК5 | Зеркало в рост в тонкой чёрной раме; рама — чёрный матовый; 600×1600 мм; низ на 300 мм от пола | | | аналог по характеристикам | шт. | 1 | 12 | пом. 6; крепление: анкер для пустотелых оснований, 4 шт. |
| ДК9 | Зеркало; рама — чёрный матовый; 800×1800 мм; низ на 550 мм от пола | | | аналог по характеристикам | шт. | 1 | 18 | пом. 8; крепление: анкер, 4 шт. |

**Допущения и предложения на листе**

Основа листа: размеры сняты с растрового плана заказчика с частичными размерами: рисунок не в масштабе, помещения выровнены по подписанным размерам мебели и проходов; контрольный обмер не выполнен (К-1); высота потолка 2700 мм принята: на плане заказчика её нет (К-2); толщины стен 300 / 120 мм приняты по плану заказчика, не замерены (К-1); разрешённая мощность 15 кВт принята по типовым ТУ для квартиры, ТУ заказчиком не переданы (К-4).

См. лист открытых вопросов (лист 6, записи К-1, К-2, К-4).

| Изм. | Кол.уч | Лист | № док. | Подп. | Дата |
|---|---|---|---|---|---|
| Разраб. | | Кырлан А.С. | | | 18.10.26 |
| Пров. | | | | | |
| ГИП | | | | | |
| | | | | | |
| Н. контр. | | | | | |
| Утв. | | | | | |

**ГД-2026-008-АИ**

Квартира с кабинетом

Общая площадь 127,29* м² · * размеры со скана, не замерены (реестр — л. 6, К-1)

| | Стадия | Лист | Листов |
|---|---|---|---|
| Дизайн-проект интерьера | РП | 19 | 92 |

**Спецификация мебели и оборудования (продолжение)**
М б/м

**Кырлан Александр Сергеевич**

03

# Электрооборудование

Кырлан Александр Сергеевич

# План розеток и электровыводов

Розетки, выводы кабеля, щит · размеры в мм · высоты от чистого пола

**ПРЕДВАРИТЕЛЬНО · не для производства работ · открыто пунктов: 4 (реестр — л. 6)**

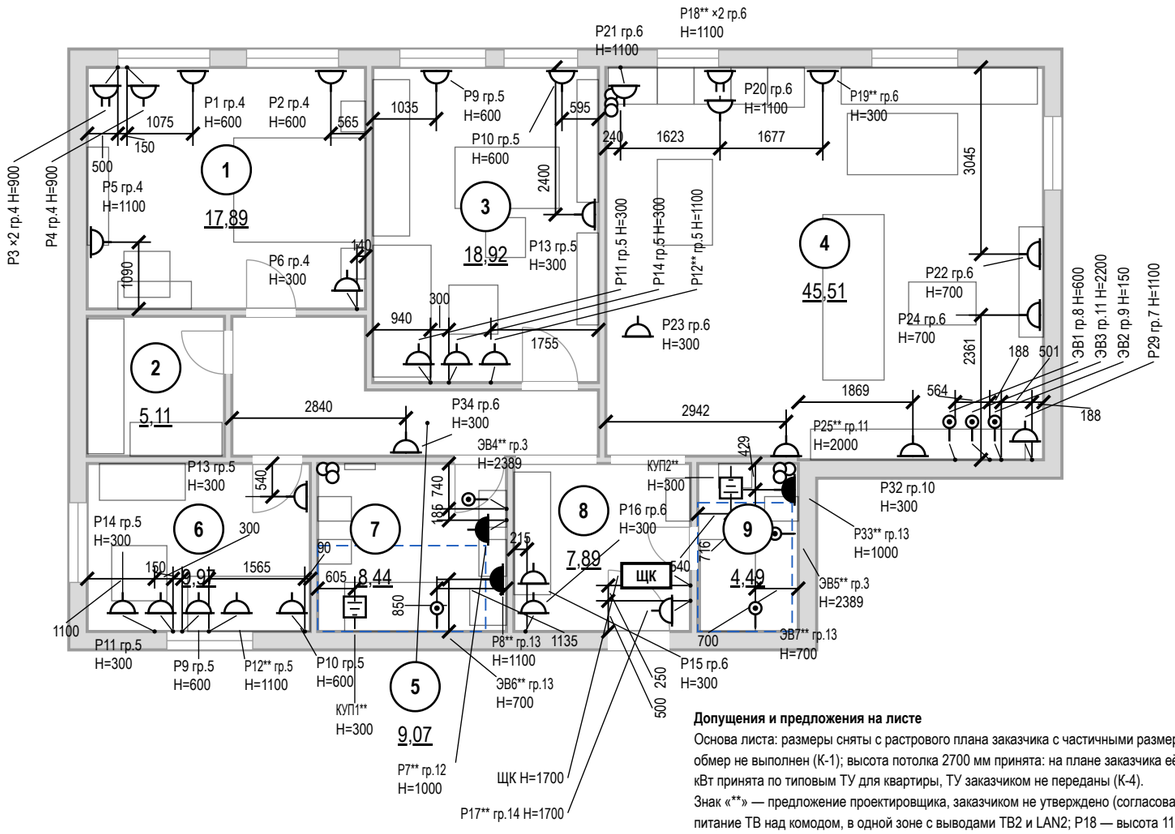


## Условные обозначения

- розетка с заземляющим контактом; у знака — марка, ×N постов в рамке, гр. — группа щита, H — высота оси, мм
- то же, рамка на 2 поста (число черточек — число постов)
- розетка влагозащищённая IP44
- вывод кабеля для подключения прибора (без розетки), марка ЭВ
- КУП — коробка уравнивания потенциалов (ДСУП), проводник к шине PE щита
- ЩК — щит квартирный
- знак разведён для читаемости: точка на стене — у выноски, привязка — до неё
- граница зоны 2 ванной (600 мм от ванны/поддона)
- мебель и сантехприборы — подложка
- стояк: К1 — канализация, В1 — ХВС, Т3 — ГВС
- 1 — номер помещения, площадь м²

**Допущения и предложения на листе**

Основа листа: размеры сняты с растрового плана заказчика с частичными размерами: рисунок не в масштабе, помещения выровнены по подписанным размерам мебели и проходов; контрольный обмер не выполнен (К-1); высота потолка 2700 мм принята: на плане заказчика её нет (К-2); толщины стен 300 / 120 мм приняты по плану заказчика, не замерены (К-1); разрешённая мощность 15 кВт принята по типовым ТУ для квартиры, ТУ заказчиком не переданы (К-4).

Знак «**» — предложение проектировщика, заказчиком не утверждено (согласовать с заказчиком): записи в реестре нет: P12 — высота 1100 мм выше нормы 1 м (ПУЭ 6.6.30) по назначению: питание ТВ над комодом, в одной зоне с выводами ТВ2 и LAN2; P18 — высота 1100 мм выше нормы 1 м (ПУЭ 6.6.30) по назначению: питание ТВ, в одной зоне с выводами ТВ1 и LAN3; P19 — высота 1100 мм выше нормы 1 м (ПУЭ 6.6.30) по назначению: питание приставки ТВ, в одной зоне с выводами ТВ1 и LAN3; P25 — высота 2000 мм выше нормы 1 м (ПУЭ 6.6.30) по назначению: питание встроенного холодильника М6, розетка над нишей за съёмной панелью; P7, P8 — по образцу: P7, P8 и P33 на высоте 1000 мм — верхний предел нормы (ПУЭ, п. 6.6.30, не выше 1 м); флаг решения снят; ЭВ4, КУП1, ЭВ5, КУП2 — по образцу: Добавлены выводы к вентиляторам: ЭВ4 (ВР1, ванная) и ЭВ5 (ВР3, санузел 2) — группа 3, высота 2389 мм, включение с основным светом, таймер выбега в вентиляторе; и коробки уравнивания потенциалов КУП1 (ванная) и КУП2 (санузел 2) — высота 300 мм, у входа, вне зон 0–2, проводник от шины PE щита ЩК, сече; ЭВ6, ЭВ7 — по образцу: Добавлены электрические полотенцесушители IP44: П10 в ванной (480 мм, низ 900 мм) и П13 в санузле 2 (400 мм, низ 900 мм), выводы ЭВ6 и ЭВ7; мощность группы 13 — 2,4 кВт вместо 1,8 кВт; P17 — высота 1700 мм выше нормы 1 м (ПУЭ 6.6.30) по назначению: питание слаботочного щита ЩС, рядом со щитом на его высоте; P33 — по образцу: Розетка P33 на высоте 1100 мм, вне шва плитки.

Открытые вопросы и конфликты по листу: К-4.

См. лист открытых вопросов (лист 6, записи К-1, К-2, К-4).

## Примечания

1. За отметку 0,000 принят уровень чистого пола. Высоты H — от чистого пола до оси изделия; привязки — от чистовой грани стены до оси механизма (у рамки на несколько постов — до оси рамки).
2. Высота установки, не указанная на плане: розетки — 300 мм от чистого пола; выводы кабеля — по паспорту прибора.
3. Розетки в санузле — только вне зон 0–2 (ПУЭ 7.1.48, ГОСТ Р 50571.7.701-2024), IP44, через УЗО 30 мА.
4. Розеточные и мокрые линии — через УЗО или дифавтомат с током утечки не более 30 мА (ПУЭ 7.1.79); в санузле выполнить ДСУП (ПУЭ 7.1.87–7.1.88).
5. Кабель — медный, исполнение нг(A)-LS (ГОСТ 31565-2012); скрытая прокладка только горизонтально и вертикально, фактические трассы зафиксировать исполнительной схемой до закрытия отделкой.
6. Расчёт нагрузок, токов КЗ, селективности и сечений — по проекту ЭОМ организации с допуском СРО; лист задаёт состав, расположение и группы.
7. Выводы кухонной техники — после утверждения проекта кухни (ориентировочно); привязки выводов даны от осей модулей гарнитура и пересматриваются вместе с проектом кухни.
8. Электрический тёплый пол проектом не предусмотрен; при решении заказчика устроить — отдельный лист «План тёплых полов»: контуры с отступом 100 мм от стен и мебели без ножек, датчик в гофре, терморегулятор, своя группа щита через УЗО 30 мА.
9. Ведомости электроточек, изделий, светильников и расшифровка клавиш — лист 23.

1000 мм · печать 1:1

| Изм. | Кол.уч | Лист | № док. | Подп. | Дата |
|---|---|---|---|---|---|
| Разраб. | | Кырлан А.С. | | | 18.10.26 |
| Пров. | | | | | |
| ГИП | | | | | |
| | | | | | |
| Н. контр. | | | | | |
| Утв. | | | | | |

**ГД-2026-008-АИ**

Квартира с кабинетом

Общая площадь 127,29* м² · * размеры со скана, не замерены (реестр — л. 6, К-1)

Дизайн-проект интерьера

| Стадия | Лист | Листов |
|---|---|---|
| РП | 20 | 92 |

**План розеток и электровыводов**

М 1:100

**Кырлан Александр Сергеевич**

выпуск 18.10.2026 · d2d5a25dca · стр. 25 из 129

# План освещения

Светильники, группы включения, извещатели · размеры в мм



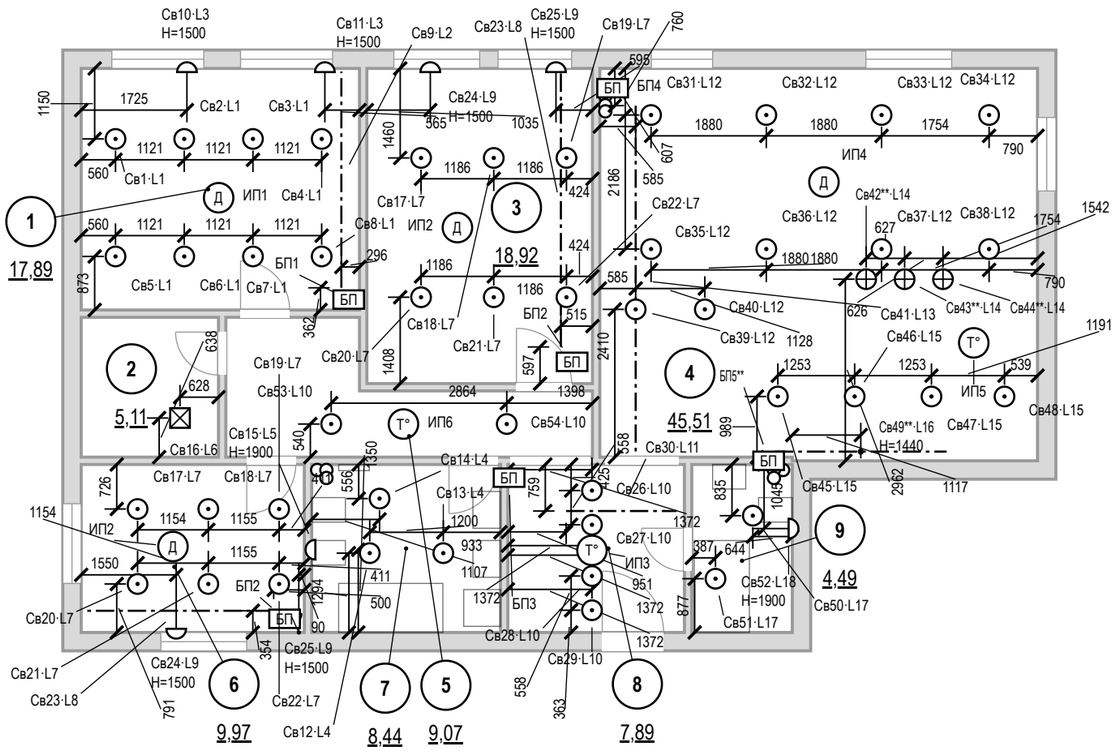


## Условные обозначения

- светильник встраиваемый точечный
- светильник потолочный накладной
- светильник подвесной
- светильник настенный (бра), H — высота оси
- линейный светильник настенный (подсветка столешницы), точка — вывод питания
- светодиодная лента в профиле / в карнизе короба
- Св1·L1 — марка светильника (как в ведомости и на развёртках) · группа включения L (лист выключателей)
- Д — извещатель пожарный дымовой автономный
- Т° — извещатель пожарный тепловой
- БП — блок питания LED, с доступом (люк от 100×100 мм)
- 1 — номер помещения, площадь м²

## Освещённость (оценка)

| Пом. | S, м² | Ен, лк | Ф треб., лм | Ф по пр., лм |
|---|---|---|---|---|
| 1 | 17,9 | 150 | 7560 | 8000 |
| 2 | 5,1 | 75 | 1080 | 900 |
| 3 | 18,9 | 300 | 15990 | 6300 |
| 4 | 45,5 | 150 | 19230 | 16000 |
| 5 | 9,1 | 50 | 1280 | 1200 |
| 6 | 10 | 200 | 5620 | 6300 |
| 7 | 8,4 | 50 | 1190 | 1500 |
| 8 | 7,9 | 50 | 1110 | 2400 |
| 9 | 4,5 | 50 | 630 | 1100 |

**Допущения и предложения на листе**

Основа листа: размеры сняты с растрового плана заказчика с частичными размерами: рисунок не в масштабе, помещения выровнены по подписанным размерам мебели и проходов; контрольный обмер не выполнен (К-1); высота потолка 2700 мм принята: на плане заказчика её нет (К-2); толщины стен 300 / 120 мм приняты по плану заказчика, не замерены (К-1); разрешённая мощность 15 кВт принята по типовым ТУ для квартиры, ТУ заказчиком не переданы (К-4).

Знак «**» — предложение проектировщика, заказчиком не утверждено (согласовать с заказчиком): записи в реестре нет: Св42, Св43, Св44, Св49, БП5 — диммируемость добавлена разработчиком проекта под светорегуляторы S11 и S12.

См. лист открытых вопросов (лист 6, записи К-1, К-2, К-4).

## Примечания

1. За отметку 0,000 принят уровень чистого пола. Высоты H — от чистого пола до оси изделия; привязки — от чистовой грани стены до оси механизма (у рамки на несколько постов — до оси рамки).
2. Высота установки, не указанная на плане: светильники — на потолке; настенные — по отметке H у знака. Привязки — до оси светильника от чистовой грани стены, по рядам.
3. Освещённость: Ен — СанПиН 1.2.3685-21, табл. 5.52 (на полу); Ф треб. = Ен·S/(U·MF) при U = 0,5 и MF = 0,71 (СП 52.13330.2016, табл. 4.3) — оценка, не светотехнический расчёт. Декоративная подсветка в Ф не входит.
4. Во влажных помещениях — светильники не ниже IP44; в зонах 0–2 ванной — по ГОСТ Р 50571.7.701-2024 (зона 1 — IPX5).
5. Розеточные и мокрые линии — через УЗО или дифавтомат с током утечки не более 30 мА (ПУЭ 7.1.79); в санузле выполнить ДСУП (ПУЭ 7.1.87–7.1.88).
6. Кабель — медный, исполнение нг(A)-LS (ГОСТ 31565-2012); скрытая прокладка только горизонтально и вертикально, фактические трассы зафиксировать исполнительной схемой до закрытия отделкой.
7. Расчёт нагрузок, токов КЗ, селективности и сечений — по проекту ЭОМ организации с допуском СРО; лист задаёт состав, расположение и группы.
8. Ведомость светильников — лист 23.

1000 мм · печать 1:1

| Изм. | Кол.уч | Лист | № док. | Подп. | Дата |
|---|---|---|---|---|---|
| Разраб. | | Кырлан А.С. | | | 18.10.26 |
| Пров. | | | | | |
| ГИП | | | | | |
| | | | | | |
| Н. контр. | | | | | |
| Утв. | | | | | |

**ГД-2026-008-АИ**

Квартира с кабинетом

Общая площадь 127,29* м² · * размеры со скана, не замерены (реестр — л. 6, К-1)

Дизайн-проект интерьера

| Стадия | Лист | Листов |
|---|---|---|
| РП | 21 | 92 |

**План освещения**

М 1:100

**Кырлан Александр Сергеевич**

выпуск 18.10.2026 № d2d5a25dca · стр. 26 из 129

# План выключателей и схема включения

Выключатели S, группы включения L, линии связи · размеры в мм

**ПРЕДВАРИТЕЛЬНО · не для производства работ · открыто пунктов: 4 (реестр — л. 6)**

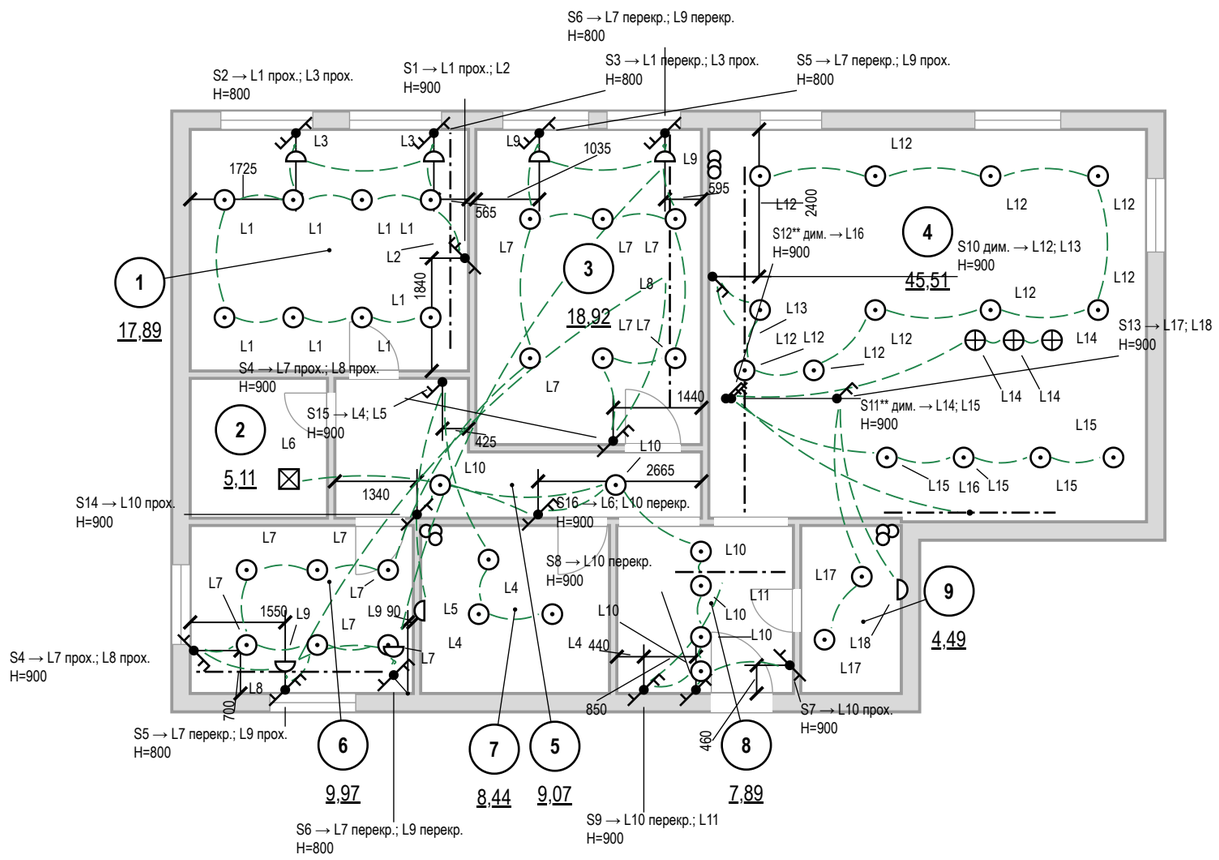


## Условные обозначения

- выключатель одноклавишный
- выключатель двухклавишный (флажков — по числу клавиш)
- выключатель с проходной или перекрёстной клавишей (обратный флажок); тип клавиши — в подписи
- S1 → — марка → группы по клавишам (через «;»): прох. — проходной, перекр. — перекрёстный, дим. — светорегулятор; Н — высота
- линия связи: выключатель → светильники группы (не трасса кабеля)
- светильник встраиваемый точечный
- светильник потолочный накладной
- светильник подвесной
- светильник настенный (бра), Н — высота оси
- линейный светильник настенный (подсветка столешницы), точка — вывод питания
- светодиодная лента в профиле / в карнизе короба
- L1 — группа включения у светильника
- 1 — номер помещения, площадь м²

**Допущения и предложения на листе**

Основа листа: размеры сняты с растрового плана заказчика с частичными размерами: рисунок не в масштабе, помещения выровнены по подписанным размерам мебели и проходов; контрольный обмер не выполнен (К-1); высота потолка 2700 мм принята: на плане заказчика её нет (К-2); толщины стен 300 / 120 мм приняты по плану заказчика, не замерены (К-1); разрешённая мощность 15 кВт принята по типовым ТУ для квартиры, ТУ заказчиком не переданы (К-4).

Знак «**» — предложение проектировщика, заказчиком не утверждено (согласовать с заказчиком): записи в реестре нет: S11, S12 — светорегулятор добавлен разработчиком проекта. См. лист открытых вопросов (лист 6, записи К-1, К-2, К-4).

## Примечания

1. За отметку 0,000 принят уровень чистого пола. Высоты Н — от чистого пола до оси изделия; привязки — от чистовой грани стены до оси механизма (у рамки на несколько постов — до оси рамки).
2. Высота установки, не указанная на плане: выключатели — 900 мм от чистого пола, со стороны дверной ручки (ПУЭ 7.1.51).
3. Линии связи показывают, какой выключатель какую группу L включает; это не трасса кабеля. Трасса — принципиальная, фактическую зафиксировать исполнительной схемой.
4. Группы из нескольких мест (L1 — S1, S2, S3; L3 — S2, S3; L7 — S4, S4, S5, S5, S6, S6; L8 — S4, S4; L9 — S5, S5, S6, S6; L10 — S7, S8, S9, S14, S16): на крайних местах — проходные клавиши, на промежуточных — перекрёстные; механизмы — в ведомости изделий.
5. Светорегулятор — по заднему фронту (для LED-драйверов), совместимость с драйверами проверить до закупки.
6. Розеточные и мокрые линии — через УЗО или дифавтомат с током утечки не более 30 мА (ПУЭ 7.1.79); в санузле выполнить ДСУП (ПУЭ 7.1.87–7.1.88).
7. Кабель — медный, исполнение нг(А)-LS (ГОСТ 31565-2012); скрытая прокладка только горизонтально и вертикально, фактические трассы зафиксировать исполнительной схемой до закрытия отделкой.
8. Расчёт нагрузок, токов КЗ, селективности и сечений — по проекту ЭОМ организации с допуском СРО; лист задаёт состав, расположение и группы.
9. Расшифровка клавиш и ведомость изделий — лист 23.

1000 мм · печать 1:1

| Изм. | Кол.уч | Лист | № док. | Подп. | Дата |
|---|---|---|---|---|---|
| Разраб. | | Кырлан А.С. | | | 18.10.26 |
| Пров. | | | | | |
| ГИП | | | | | |
| | | | | | |
| Н. контр. | | | | | |
| Утв. | | | | | |

**ГД-2026-008-АИ**

Квартира с кабинетом

Общая площадь 127,29* м² · * размеры со скана, не замерены (реестр — л. 6, К-1)

Дизайн-проект интерьера

| Стадия | Лист | Листов |
|---|---|---|
| РП | 22 | 92 |

**План выключателей и схема включения**

М 1:100

**Кырлан Александр Сергеевич**

выпуск 18.10.2026 № d2d5a25dca · стр. 27 из 129

# Ведомость электроточек и изделий

Электроточки, изделия, светильники, клавиши выключателей · б/м

## Ведомость электроточек

| Марка | Пом. | Назначение | H, мм | Гр. |
|---|---|---|---|---|
| Р1 | 1 | у кровати | 600 | 4 |
| Р2 | 1 | у кровати | 600 | 4 |
| Р3 | 1 | рабочий стол | 900 | 4 |
| Р4 | 1 | рабочий стол | 900 | 4 |
| Р5 | 1 | торшер у кресла | 1100 | 4 |
| Р6 | 1 | уборка | 300 | 4 |
| Р9 | 3 | у кровати | 600 | 5 |
| Р10 | 3 | у кровати | 600 | 5 |
| Р11 | 3 | у комода | 300 | 5 |
| Р12** | 3 | ТВ над комодом (в одной зоне с ТВ2, LAN2) | 1100 | 5 |
| Р13 | 3 | уборка | 300 | 5 |
| Р14 | 3 | уборка у входа | 300 | 5 |
| Р18** | 4 | ТВ (в одной зоне с ТВ1, LAN3) | 1100 | 6 |
| Р19** | 4 | ТВ-приставка (в одной зоне с ТВ1, LAN3) | 300 | 6 |
| Р20 | 4 | у ТВ-тумбы | 1100 | 6 |
| Р21 | 4 | торшер | 1100 | 6 |
| Р22 | 4 | у кресла | 700 | 6 |
| Р23 | 4 | уборка, пылесос | 300 | 6 |
| Р24 | 4 | у обеденного стола | 700 | 6 |
| Р25** | 4 | холодильник, над нишей М6 (съёмная панель) | 2000 | 11 |
| Р29 | 4 | фартук | 1100 | 7 |
| Р32 | 4 | посудомоечная машина | 300 | 10 |
| ЭВ1 | 4 | варочная панель (в соседнем модуле М8.3, за ящиком) | 600 | 8 |
| ЭВ2 | 4 | духовой шкаф | 150 | 9 |
| ЭВ3 | 4 | вытяжка | 2200 | 11 |
| Р34 | 5 | уборка | 300 | 6 |
| Р9 | 6 | у кровати | 600 | 5 |
| Р10 | 6 | у кровати | 600 | 5 |
| Р11 | 6 | у комода | 300 | 5 |
| Р12** | 6 | ТВ над комодом (в одной зоне с ТВ2, LAN2) | 1100 | 5 |

## Ведомость электроточек (продолжение)

| Марка | Пом. | Назначение | H, мм | Гр. |
|---|---|---|---|---|
| Р13 | 6 | уборка | 300 | 5 |
| Р14 | 6 | уборка у входа | 300 | 5 |
| КУП1** | 7 | КУП — уравнивание потенциалов (ДСУП) | 300 | |
| Р7** | 7 | стиральная машина, IP44 | 1000 | 12 |
| Р8** | 7 | фен у умывальника, IP44 | 1100 | 13 |
| ЭВ4** | 7 | вентилятор ВР1 (таймер выбега) | 2389 | 3 |
| ЭВ6** | 7 | полотенцесушитель П10, IP44 | 700 | 13 |
| Р15 | 8 | пылесос, сушилка обуви | 300 | 6 |
| Р16 | 8 | уборка | 300 | 6 |
| Р17** | 8 | питание слаботочного щита (рядом с ЩС**) | 1700 | 14 |
| ЩК | 8 | щит квартирный ЩРВ-П-48 | 1700 | |
| КУП2** | 9 | КУП — уравнивание потенциалов (ДСУП) | 300 | |
| Р33** | 9 | фен у умывальника, IP44 | 1000 | 13 |
| ЭВ5** | 9 | вентилятор ВР3 (таймер выбега) | 2389 | 3 |
| ЭВ7** | 9 | полотенцесушитель П13, IP44 | 700 | 13 |

## Ведомость изделий

| Наименование | Марки | Ед. | Кол. |
|---|---|---|---|
| Розетка с з/к и защитными шторками, 16 А | по ведомости точек | шт | 34 |
| Розетка IP44 с крышкой, 16 А | Р7**, Р8**, Р33** | шт | 3 |
| Выключатель 1-клав. перекрёстный | S8 | шт | 1 |
| Выключатель 1-клав. проходной | S7, S14 | шт | 2 |
| Выключатель 2-клав. | S13, S15 | шт | 2 |
| Выключатель 2-клав. (перекрёстная + обычная) | S9, S16 | шт | 2 |
| Выключатель 2-клав. (перекрёстная + проходная) | S3, S5 | шт | 3 |
| Выключатель 2-клав. (проходная + обычная) | S1 | шт | 1 |
| Выключатель 2-клав. перекрёстный | S6 | шт | 2 |
| Выключатель 2-клав. проходной | S2, S4 | шт | 3 |
| Светорегулятор 1-канальный, задний фронт (LED) | S12** | шт | 1 |
| Светорегулятор 2-канальный, задний фронт (LED) | S10, S11** | шт | 2 |

## Ведомость изделий (продолжение)

| Наименование | Марки | Ед. | Кол. |
|---|---|---|---|
| Датчик движения ночной подсветки | L11 | шт | 1 |
| Рамка 1-постовая | в т. ч. 19 под выключ. | шт | 52 |
| Рамка 2-постовая | | шт | 2 |
| Коробка установочная (подрозетник) Ø68 | розетки, выключатели | шт | 56 |
| Вывод кабеля под прибор (клеммник) | ЭВ1–ЭВ3, ЭВ4**, ЭВ5**, ЭВ6**, ЭВ7** | шт | 7 |
| Коробка уравнивания потенциалов КУП | КУП1**, КУП2** | шт | 2 |
| Блок питания LED 24 В, 200 Вт, дим. | БП1, БП2 | шт | 3 |
| Блок питания LED 24 В, 300 Вт, дим. | БП4 | шт | 1 |
| Блок питания LED 24 В, 60 Вт, дим. | БП5** | шт | 1 |
| Блок питания LED 24 В, 20 Вт | БП3 | шт | 1 |
| Извещатель дымовой автономный | ИП1, ИП2, ИП4 | шт | 4 |
| Извещатель тепловой | ИП3, ИП5, ИП6 | шт | 3 |
| Щит квартирный (состав — лист щита) | ЩК | шт | 1 |
| Розетка компьютерная RJ45, кат. 6, с рамкой и подрозетником | LAN1–LAN3 | шт | 4 |
| Розетка телевизионная (коаксиальная) с рамкой и подрозетником | ТВ1, ТВ2 | шт | 3 |
| Точка доступа Wi-Fi (оборудование заказчика), питание PoE | АР1**, АР2** | шт | 2 |
| Трубка или монитор домофона (поставка домофонной организации) | ДФ1 | шт | 1 |
| Щит слаботочный ЩС**: корпус, DIN-рейка, розетки 220 В | ЩС** | шт | 1 |
| Патч-панель, портов не менее 6 | | шт | 1 |
| Коммутатор, портов не менее 6, из них PoE 2 | | шт | 1 |
| Кабель домофона — тип по системе поставщика (по лучам от ЩС**, запас 10 %) | | м | 5,7 |
| Кабель коаксиальный RG-6 (75 Ом) к розеткам ТВ (по лучам от ЩС**, запас 10 %) | | м | 52,5 |
| Кабель U/UTP кат. 6 (LAN, Wi-Fi и камеры по PoE) (по лучам от ЩС**, запас 10 %) | | м | 97 |

## Ведомость светильников

| Поз. | Марки | Тип | Кол. | P, Вт | Ф, лм | IP | Тц/Ra |
|---|---|---|---|---|---|---|---|
| 1 | Св1–Св8 | встраиваемый точечный | 8 | 12 | 1000 | | 2700/90 |
| 2 | Св9 | светодиодная лента, 15,5 м | 1 | 148,8 | 13950 | | 2700/90 |
| 3 | Св10, Св11, Св24, Св25 | настенный (бра), H=1500 | 6 | 6 | 400 | | 2700/90 |
| 4 | Св16 | потолочный накладной | 1 | 10 | 900 | | 3000/90 |
| 5 | Св17–Св22 | встраиваемый точечный | 12 | 12 | 1050 | | 2700/90 |
| 6 | Св23 | светодиодная лента, 12,3 м | 2 | 118,1 | 11070 | | 2700/90 |
| 7 | Св31–Св40 | встраиваемый точечный | 10 | 12 | 1000 | | 3000/90 |
| 8 | Св41 | светодиодная лента, 22,1 м | 1 | 212,2 | 19890 | | 2700/90 |
| 9 | Св42**, Св43**, Св44** | подвесной | 3 | 9 | 800 | | 3000/90 |
| 10 | Св45–Св48 | встраиваемый точечный | 4 | 10 | 900 | | 3000/90 |
| 11 | Св49** | линейный светильник, H=1440 | 1 | 18 | 1500 | | 3000/90 |
| 12 | Св26–Св29, Св53, Св54 | встраиваемый точечный | 6 | 7 | 600 | | 3000/90 |
| 13 | Св12–Св14, Св51 | встраиваемый точечный | 4 | 6 | 500 | 44 | 3000/90 |
| 14 | Св15, Св52 | настенный (бра), H=1900 | 2 | 8 | 600 | 44 | 3000/90 |
| 15 | Св30 | светодиодная лента, 1,8 м | 1 | 8,6 | 270 | | 2700/90 |
| 16 | Св50 | встраиваемый точечный | 1 | 7 | 600 | 44 | 3000/90 |

## Расшифровка клавиш

| Марка | Пом. | H, мм | Клав. | Механизм | Группа: светильники |
|---|---|---|---|---|---|
| S1 | 1 | 900 | 1 | проходной | L1: Св1–Св8 |
| | | | 2 | обычный | L2: Св9 |
| S2 | 1 | 800 | 1 | проходной | L1: Св1–Св8 |
| | | | 2 | проходной | L3: Св10, Св11 |
| S3 | 1 | 800 | 1 | перекрёстный | L1: Св1–Св8 |
| | | | 2 | проходной | L3: Св10, Св11 |
| S4 | 3 | 900 | 1 | проходной | L7: Св17–Св22 |
| | | | 2 | проходной | L8: Св23 |

## Примечания

1. Ведомости сведены с планов розеток, освещения и выключателей; марки, группы и высоты — те же, что у знаков на планах.
2. Механизмы, рамки и светорегуляторы — одной серии; число постов и клавиш сверено с выбранной серией. Перекрёстная клавиша — отдельный механизм серии.
3. За отметку 0,000 принят уровень чистого пола. Высоты H — от чистого пола до оси изделия; привязки — от чистовой грани стены до оси механизма (у рамки на несколько постов — до оси рамки).
4. Розеточные и мокрые линии — через УЗО или дифавтомат с током утечки не более 30 мА (ПУЭ 7.1.79); в санузле выполнить ДСУП (ПУЭ 7.1.87–7.1.88).
5. Кабель — медный, исполнение нг(А)-LS (ГОСТ 31565-2012); скрытая прокладка только горизонтально и вертикально, фактические трассы зафиксировать исполнительной схемой до закрытия отделкой.
6. Расчёт нагрузок, токов КЗ, селективности и сечений — по проекту ЭОМ организации с допуском СРО; лист задаёт состав, расположение и группы.
7. Ведомости занимают 2 листов этого наименования: таблицы, не вошедшие в поле листа, продолжены на следующем листе.

Допущения и предложения на листе. Знак «**» предложено (согласовать). См. лист открытых вопросов (лист 6).

| Изм. | Кол.уч | Лист | № док. | Подп. | Дата |
|---|---|---|---|---|---|
| Разраб. | | Кырлан А.С. | | | 18.10.26 |
| Пров. | | | | | |
| ГИП | | | | | |
| | | | | | |
| Н. контр. | | | | | |
| Утв. | | | | | |

**ГД-2026-008-АИ**

Квартира с кабинетом

Общая площадь 127,29* м² · * размеры со скана, не замерены (реестр — л. 6, К-1)

Дизайн-проект интерьера

| Стадия | Лист | Листов |
|---|---|---|
| РП | 23 | 92 |

**Ведомость электроточек и изделий**

М б/м

**Кырлан Александр Сергеевич**

выпуск 18.10.2026 № d2d5a25dca · стр. 28 из 129

# Ведомость электроточек и изделий (продолжение)

Электроточки, изделия, светильники, клавиши выключателей · б/м

## Расшифровка клавиш (продолжение)

| Марка | Пом. | Н, мм | Клав. | Механизм | Группа: светильники |
|---|---|---|---|---|---|
| S4 | 6 | 900 | 1 | проходной | L7: Св17–Св22 |
| | | | 2 | проходной | L8: Св23 |
| S5 | 3 | 800 | 1 | перекрёстный | L7: Св17–Св22 |
| | | | 2 | проходной | L9: Св24, Св25 |
| S5 | 6 | 800 | 1 | перекрёстный | L7: Св17–Св22 |
| | | | 2 | проходной | L9: Св24, Св25 |
| S6 | 3 | 800 | 1 | перекрёстный | L7: Св17–Св22 |
| | | | 2 | перекрёстный | L9: Св24, Св25 |
| S6 | 6 | 800 | 1 | перекрёстный | L7: Св17–Св22 |
| | | | 2 | перекрёстный | L9: Св24, Св25 |
| S7 | 8 | 900 | 1 | проходной | L10: Св26–Св29, Св53, Св54 |
| S8 | 8 | 900 | 1 | перекрёстный | L10: Св26–Св29, Св53, Св54 |
| S9 | 8 | 900 | 1 | перекрёстный | L10: Св26–Св29, Св53, Св54 |
| | | | 2 | обычный | L11: Св30 |
| S10 | 4 | 900 | 1 | светорегулятор | L12: Св31–Св40 |
| | | | 2 | светорегулятор | L13: Св41 |
| S11** | 4 | 900 | 1 | светорегулятор | L14: Св42**, Св43**, Св44** |
| | | | 2 | светорегулятор | L15: Св45–Св48 |
| S12** | 4 | 900 | 1 | светорегулятор | L16: Св49** |
| S13 | 4 | 900 | 1 | обычный | L17: Св50, Св51 |
| | | | 2 | обычный | L18: Св52 |
| S14 | 5 | 900 | 1 | проходной | L10: Св26–Св29, Св53, Св54 |
| S15 | 5 | 900 | 1 | обычный | L4: Св12–Св14 |
| | | | 2 | обычный | L5: Св15 |
| S16 | 5 | 900 | 1 | обычный | L6: Св16 |
| | | | 2 | перекрёстный | L10: Св26–Св29, Св53, Св54 |

**Допущения и предложения на листе**

Основа листа: размеры сняты с растрового плана заказчика с частичными размерами: рисунок не в масштабе, помещения выровнены по подписанным размерам мебели и проходов; контрольный обмер не выполнен (К-1); высота потолка 2700 мм принята: на плане заказчика её нет (К-2); толщины стен 300 / 120 мм приняты по плану заказчика, не замерены (К-1); разрешённая мощность 15 кВт принята по типовым ТУ для квартиры, ТУ заказчиком не переданы (К-4).

Знак «**» — предложение проектировщика, заказчиком не утверждено (согласовать с заказчиком): записи в реестре нет: S11, S12 — светорегулятор добавлен разработчиком проекта; Св42, Св43, Св44, Св49 — диммируемость добавлена разработчиком проекта под светорегуляторы S11 и S12.

См. лист открытых вопросов (лист 6, записи К-1, К-2, К-4).

## Примечания

1. Продолжение ведомостей: лист 2 из 2 этого наименования; таблицы, прерванные на предыдущем листе, продолжены с заголовком «(продолжение)».
2. За отметку 0,000 принят уровень чистого пола. Высоты Н — от чистого пола до оси изделия; привязки — от чистовой грани стены до оси механизма (у рамки на несколько постов — до оси рамки).
3. Розеточные и мокрые линии — через УЗО или дифавтомат с током утечки не более 30 мА (ПУЭ 7.1.79); в санузле выполнить ДСУП (ПУЭ 7.1.87–7.1.88).
4. Кабель — медный, исполнение нг(А)-LS (ГОСТ 31565-2012); скрытая прокладка только горизонтально и вертикально, фактические трассы зафиксировать исполнительной схемой до закрытия отделкой.
5. Расчёт нагрузок, токов КЗ, селективности и сечений — по проекту ЭОМ организации с допуском СРО; лист задаёт состав, расположение и группы.

| Изм. | Кол.уч | Лист | № док. | Подп. | Дата |
|---|---|---|---|---|---|
| Разраб. | | Кырлан А.С. | | | 18.10.26 |
| Пров. | | | | | |
| ГИП | | | | | |
| | | | | | |
| Н. контр. | | | | | |
| Утв. | | | | | |

**ГД-2026-008-АИ**

Квартира с кабинетом

Общая площадь 127,29* м² · * размеры со скана, не замерены (реестр — л. 6, К-1)

Дизайн-проект интерьера

| Стадия | Лист | Листов |
|---|---|---|
| РП | 24 | 92 |

**Ведомость электроточек и изделий (продолжение)**
М б/м

**Кырлан Александр Сергеевич**

выпуск 18.10.2026 № d2d5a25dca · стр. 29 из 129

# Однолинейная схема щита

Щит квартирный ЩК · без масштаба

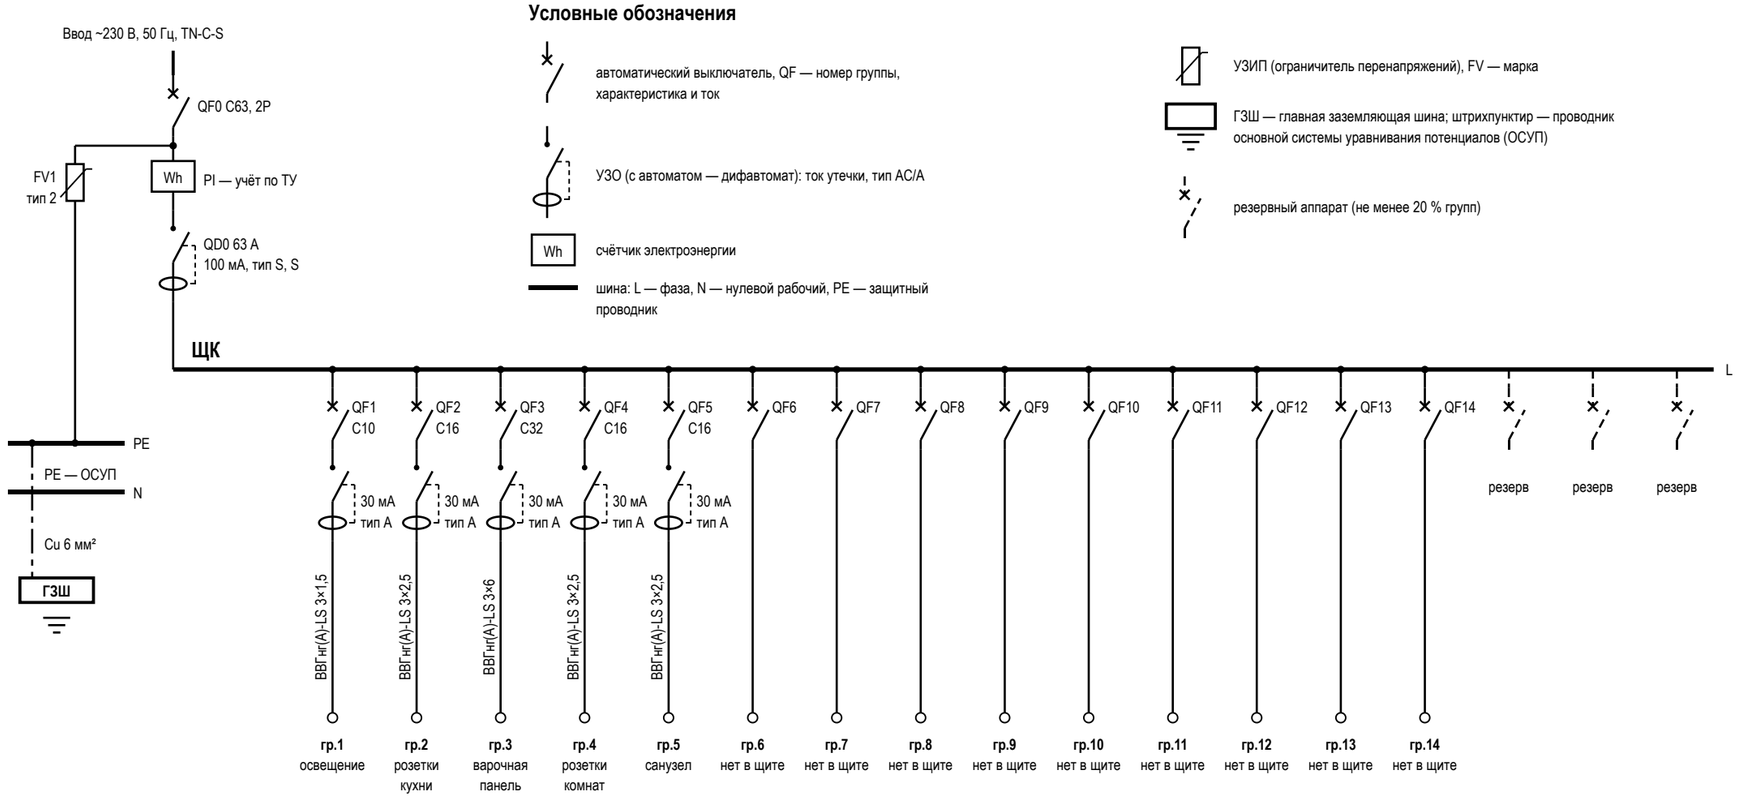


## Условные обозначения

- автоматический выключатель, QF — номер группы, характеристика и ток
- УЗО (с автоматом — дифавтомат): ток утечки, тип AC/A
- Wh — счётчик электроэнергии
- шина: L — фаза, N — нулевой рабочий, PE — защитный проводник
- УЗИП (ограничитель перенапряжений), FV — марка
- ГЗШ — главная заземляющая шина; штрихпунктир — проводник основной системы уравнивания потенциалов (ОСУП)
- резервный аппарат (не менее 20 % групп)

## Данные щитка

| Показатель | Значение |
|---|---|
| Номер щитка | ЩК |
| Тип | ЩРВ-П-24, IP41 |
| Уст. мощность, кВт | |
| Разреш. мощность, кВт | 15 |
| Расчётная, кВт | 9,8 |
| Автоматы 1п: занят. / рез. | 5 / 3 |
| Модулей: всего / занято | 24 / 16 |
| Ток на вводе, А | 63 |
| Вводной аппарат | QF0 C63, 2P |
| УЗИП | FV1, тип 2, ЩК, после счётчика |
| ГЗШ, проводник ОСУП | Cu 6 мм² |

## Таблица групп щита ЩК и кабельный журнал

| № | Назначение | Помещения | Автомат | УЗО / дифавтомат | Кабель | Длина, м | Р, кВт | Точек |
|---|---|---|---|---|---|---|---|---|
| 1 | освещение | 1, 2, 3, 5, 6 | C10 | 30 мА, тип A | ВВГнг(A)-LS 3×1,5 | 143,7 | | 43 |
| 2 | розетки кухни | 4, 5, 8 | C16 | 30 мА, тип A | ВВГнг(A)-LS 3×2,5 | 101,5 | | 36 |
| 3 | варочная панель | 4, 5, 7, 9 | C32 | 30 мА, тип A | ВВГнг(A)-LS 3×6 | 45,3 | | 11 |
| 4 | розетки комнат | 1 | C16 | 30 мА, тип A | ВВГнг(A)-LS 3×2,5 | 38,4 | | 6 |
| 5 | санузел | 3, 6 | C16 | 30 мА, тип A | ВВГнг(A)-LS 3×2,5 | 51,5 | | 12 |
| 6 | нет в щите | 4, 5, 8 | | | | | | 10 |
| 7 | нет в щите | 4 | | | | | | 1 |
| 8 | нет в щите | 4 | | | | | | 1 |
| 9 | нет в щите | 4 | | | | | | 1 |
| 10 | нет в щите | 4 | | | | | | 1 |
| 11 | нет в щите | 4 | | | | | | 2 |
| 12 | нет в щите | 7 | | | | | | 1 |
| 13 | нет в щите | 7, 9 | | | | | | 4 |
| 14 | нет в щите | 8 | | | | | | 1 |
| | Итого по сечениям ВВГнг(A)-LS, м: 3×1,5 — 143,7; 3×2,5 — 191,4; 3×6 — 45,3 | | | | | 380,4 | | |

**Допущения и предложения на листе**

Основа листа: размеры сняты с растрового плана заказчика с частичными размерами: рисунок не в масштабе, помещения выровнены по подписанным размерам мебели и проходов; контрольный обмер не выполнен (К-1); высота потолка 2700 мм принята: на плане заказчика её нет (К-2); толщины стен 300 / 120 мм приняты по плану заказчика, не замерены (К-1); разрешённая мощность 15 кВт принята по типовым ТУ для квартиры, ТУ заказчиком не переданы (К-4).

Открытые вопросы и конфликты по листу: К-4.

См. лист открытых вопросов (лист 6, записи К-1, К-2, К-4).

## Примечания

1. Схема однолинейная: одна линия — фаза, N и PE группы; аппараты — в отключённом положении (ГОСТ 2.702, ГОСТ 2.755). Номера групп — как у точек на планах (гр.). За отметку 0,000 принят уровень чистого пола; высота щита — по плану розеток.
2. Розеточные и мокрые линии — через УЗО или дифавтомат с током утечки не более 30 мА (ПУЭ 7.1.79); в санузле выполнить ДСУП (ПУЭ 7.1.87–7.1.88).
3. УЗО тип A — для линий с электроникой, стиральной и посудомоечной машиной, LED-драйверами; тип AC — только для чисто активной нагрузки.
4. Кабель — медный, исполнение нг(A)-LS (ГОСТ 31565-2012); скрытая прокладка только горизонтально и вертикально, фактические трассы зафиксировать исполнительной схемой до закрытия отделкой.
5. Номинал автомата — не выше допустимого тока кабеля: 1,5 мм² — до 10 А, 2,5 мм² — до 16 А. Резерв щита — не менее 20 % модулей.
6. Расчёт нагрузок, токов КЗ, селективности и сечений — по проекту ЭОМ организации с допуском СРО; лист задаёт состав, расположение и группы.
7. УЗИП FV1 — после вводного автомата, проводник к шине PE — кратчайший, без петель. Шина PE щита соединяется с ГЗШ проводником ОСУП; к ГЗШ присоединяются трубы водопровода и отопления на вводе в квартиру (ПУЭ 7.1.87). Шины N и PE — раздельные, после разделения PEN не объединяются.
8. До подключения нагрузки — приёмо-сдаточные испытания с протоколом: сопротивление изоляции линий не менее 0,5 МОм, срабатывание УЗО по току и времени, непрерывность защитных проводников PE (ПУЭ, гл. 1.8).
9. Группы с пометкой «нет в щите» есть на планах, но не описаны в щите — дополнить аппаратами до закупки.

| Изм. | Кол.уч | Лист | № док. | Подп. | Дата |
|---|---|---|---|---|---|
| Разраб. | | Кырлан А.С. | | | 18.10.26 |
| Пров. | | | | | |
| ГИП | | | | | |
| | | | | | |
| Н. контр. | | | | | |
| Утв. | | | | | |

**ГД-2026-008-АИ**

Квартира с кабинетом

Общая площадь 127,29* м² · * размеры со скана, не замерены (реестр — л. 6, К-1)

Дизайн-проект интерьера

| Стадия | Лист | Листов |
|---|---|---|
| РП | 25 | 92 |

**Однолинейная схема щита**

М б/м

**Кырлан Александр Сергеевич**

# План принципиальных трасс

Силовые трассы и объёмы электромонтажа, слаботочка в объёмах · размеры в мм

**ПРЕДВАРИТЕЛЬНО · не для производства работ · открыто пунктов: 4 (реестр — л. 6)**

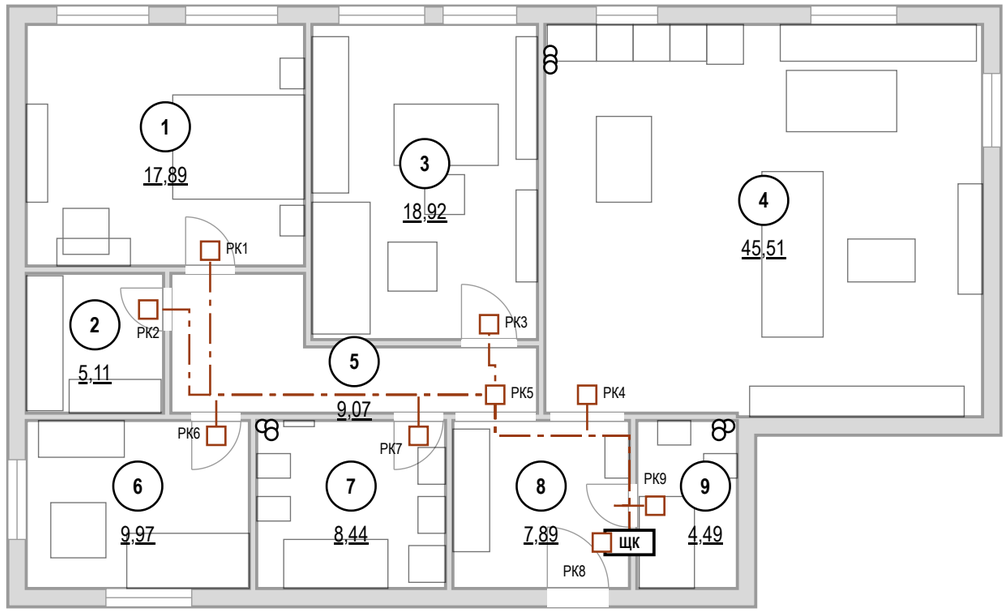


## Кабель по группам ВВГнг(А)-LS, м

| Гр. | мм² | Трасса | Данные |
|---|---|---|---|
| 1 | 3×1,5 | 143,7 | |
| 2 | 3×2,5 | 101,5 | |
| 3 | 3×6 | 45,3 | |

| Гр. | мм² | Трасса | Данные |
|---|---|---|---|
| 4 | 3×2,5 | 38,4 | |
| 5 | 3×2,5 | 51,5 | |
| **Σ** | | **380,4** | |

## Экспликация помещений

| № | Помещение | Площадь, м² |
|---|---|---|
| 1 | Спальня | 17,89 |
| 2 | Гардеробная-постирочная | 5,11 |
| 3 | Кабинет | 18,92 |
| 4 | Кухня-гостиная | 45,51 |
| 5 | Коридор | 9,07 |
| 6 | Детская | 9,97 |
| 7 | Ванная | 8,44 |
| 8 | Прихожая | 7,89 |
| 9 | Санузел гостевой | 4,49 |
| | Итого (общая площадь) | 127,29 |

## Объёмы прокладки

| Работа, материал | Ед. | Кол. |
|---|---|---|
| Гофротруба Ø20 в потолочном пространстве | м | 167,9 |
| Кабель-канал плинтуса для силовых линий | м | 87,2 |
| Короб или накладной канал для вертикальных спусков и подъёмов | м | 60,3 |
| Коробка распределительная (РК) над дверью помещения | шт | 9 |
| Слаботочка: кабель домофона | м | 5,7 |
| Слаботочка: Кабель коаксиальный RG-6 (75 Ом) к розеткам ТВ | м | 52,5 |
| Слаботочка: U/UTP кат. 6 (LAN, Wi-Fi, камеры) | м | 97 |
| Слаботочка: гофротруба Ø20 отдельно от силовых | м | 139,7 |

## Штробы — только после заключения

| Работа | Ед. | Кол. |
|---|---|---|
| Вертикальные штробы 20×20 мм от потолка до каждой настенной точки (в маршрут без штроб не входят) | м | 119,58 |

## Условные обозначения

- **ЩК** — щит квартирный
- РК — распределительная коробка над дверью помещения
- магистраль от щита к РК: потолочное пространство, гофра
- мебель и сантехприборы — подложка

**Допущения и предложения на листе**

Основа листа: размеры сняты с растрового плана заказчика с частичными размерами: рисунок не в масштабе, помещения выровнены по подписанным размерам мебели и проходов; контрольный обмер не выполнен (К-1); высота потолка 2700 мм принята: на плане заказчика её нет (К-2); толщины стен 300 / 120 мм приняты по плану заказчика, не замерены (К-1); разрешённая мощность 15 кВт принята по типовым ТУ для квартиры, ТУ заказчиком не переданы (К-4).

Знак «**» — предложение проектировщика, заказчиком не утверждено (согласовать с заказчиком): записи в реестре нет: ЩС — щит слаботочный: место и состав. См. лист открытых вопросов (лист 6, записи К-1, К-2, К-4).

## Примечания

1. За отметку 0,000 принят уровень чистого пола. Высоты Н — от чистого пола до оси изделия; привязки — от чистовой грани стены до оси механизма (у рамки на несколько постов — до оси рамки).
2. Розеточные и мокрые линии — через УЗО или дифавтомат с током утечки не более 30 мА (ПУЭ 7.1.79); в санузле выполнить ДСУП (ПУЭ 7.1.87–7.1.88).
3. Кабель — медный, исполнение нг(А)-LS (ГОСТ 31565-2012); скрытая прокладка только горизонтально и вертикально, фактические трассы зафиксировать исполнительной схемой до закрытия отделкой.
4. Расчёт нагрузок, токов КЗ, селективности и сечений — по проекту ЭОМ организации с допуском СРО; лист задаёт состав, расположение и группы.
5. Длины — по плану: от щита вверх в потолочное пространство, по дверям и коридору без захода в мокрые помещения к распределительной коробке над дверью, далее к точкам; вертикали считаются вниз и обратно (у последней точки цепочки — в один конец); запас 10 %. Трассы принципиальные: фактическую зафиксировать исполнительной схемой до закрытия отделкой.
6. Несущие стены не определены: штробы в стенах не выполнять. Маршрут проложен без штроб: горизонтали — за потолком в гофре (167,9 м) и в кабель-канале плинтуса (87,2 м), вертикали — в коробе или накладном канале (106,1 м кабеля). Точек: за потолком — 58, спуск из потолка — 13, по плинтусу — 7, плинтус и подъём — 30.
7. Вариант со штробами — работа после технического заключения: 119,58 м вертикальных штроб от потолка до каждой настенной точки; условие — только после технического заключения: стена не несущая (или вертикальная штроба в несущей согласована конструктором), глубина и ширина 20–25 мм, не в зонах 0–2 ванной. Без заключения и согласования конструктора в смету и в график эта работа не входит.
8. Слаботочные сети: кабели и точки считаются по лучам от ЩС** (лист слаботочных сетей): 155 м, портов патч-панели и коммутатора не менее 6; из точек 2 предложения листа слаботочки, не подтверждённые заказчиком. Изделия — в ведомости изделий.

1000 мм · печать 1:1

| Изм. | Кол.уч | Лист | № док. | Подп. | Дата |
|---|---|---|---|---|---|
| Разраб. | | Кырлан А.С. | | | 18.10.26 |
| Пров. | | | | | |
| ГИП | | | | | |
| Н. контр. | | | | | |
| Утв. | | | | | |

**ГД-2026-008-АИ**

Квартира с кабинетом

Общая площадь 127,29* м² · * размеры со скана, не замерены (реестр — л. 6, К-1)

Дизайн-проект интерьера

| Стадия | Лист | Листов |
|---|---|---|
| РП | 26 | 92 |

**План принципиальных трасс**

М 1:100

**Кырлан Александр Сергеевич**

выпуск 18.10.2026 № d2d5a25dca · стр. 31 из 129

# План слаботочных сетей

Интернет, ТВ, домофон · размеры в мм · высоты от чистого пола

**ПРЕДВАРИТЕЛЬНО · не для производства работ · открыто пунктов: 4 (реестр — л. 6)**

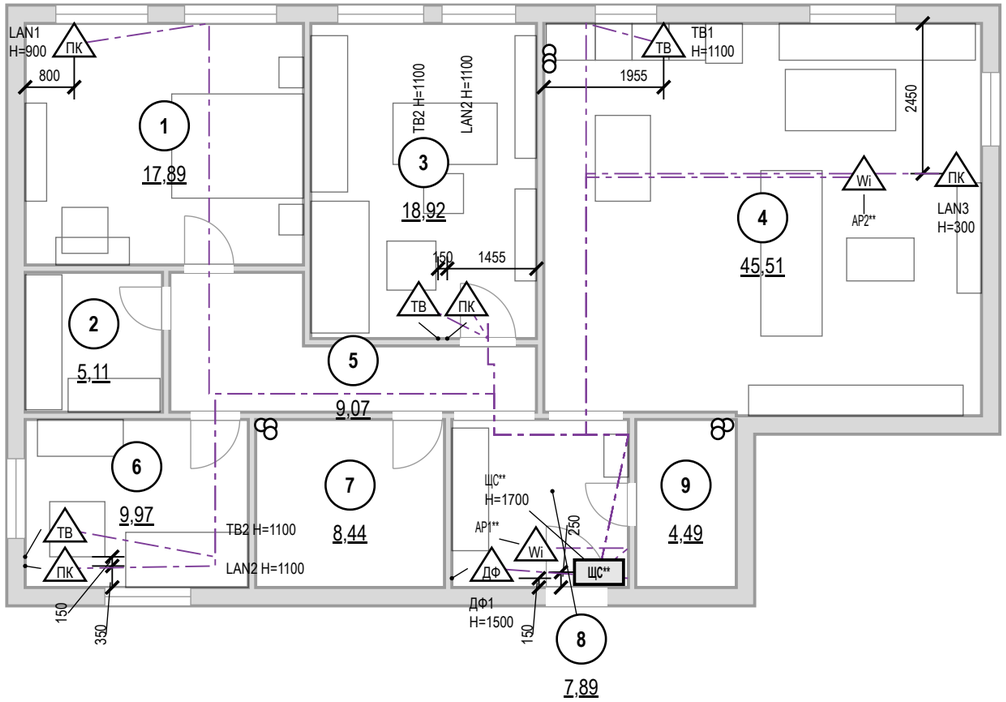


## Ведомость слаботочных точек

| Марка | Пом. | Назначение | H, мм | Кабель |
|---|---|---|---|---|
| LAN1 | 1 | розетка LAN (RJ45) | 900 | U/UTP кат. 6 |
| TB2 | 3 | розетка ТВ | 1100 | RG-6 |
| LAN2 | 3 | розетка LAN (RJ45) | 1100 | U/UTP кат. 6 |
| TB1 | 4 | розетка ТВ | 1100 | RG-6 |
| LAN3 | 4 | розетка LAN (RJ45) | 300 | U/UTP кат. 6 |
| AP2** | 4 | точка доступа Wi-Fi | | U/UTP кат. 6 |
| TB2 | 6 | розетка ТВ | 1100 | RG-6 |
| LAN2 | 6 | розетка LAN (RJ45) | 1100 | U/UTP кат. 6 |
| ЩС** | 8 | щит слаботочный | 1700 | ввод пров. |
| ДФ1 | 8 | домофон (трубка) | 1500 | по системе |
| AP1** | 8 | точка доступа Wi-Fi | | U/UTP кат. 6 |

## Условные обозначения

- **ЩС** — щит слаботочный: ввод провайдера, роутер, коммутатор
- ПК — розетка компьютерная RJ45
- ТВ — розетка телевизионная
- ДФ — трубка или монитор домофона
- Wi — точка доступа Wi-Fi (питание PoE)
- кабель от ЩС до точки, отдельным лучом
- мебель и сантехприборы — подложка
- 1 — номер помещения, площадь м²

**Допущения и предложения на листе**

Основа листа: размеры сняты с растрового плана заказчика с частичными размерами: рисунок не в масштабе, помещения выровнены по подписанным размерам мебели и проходов; контрольный обмер не выполнен (К-1); высота потолка 2700 мм принята: на плане заказчика её нет (К-2); толщины стен 300 / 120 мм приняты по плану заказчика, не замерены (К-1); разрешённая мощность 15 кВт принята по типовым ТУ для квартиры, ТУ заказчиком не переданы (К-4).

Знак «**» — предложение проектировщика, заказчиком не утверждено (согласовать с заказчиком): записи в реестре нет: AP2, AP1 — точка доступа Wi-Fi: число и места; ЩС — щит слаботочный: место и состав.

См. лист открытых вопросов (лист 6, записи К-1, К-2, К-4).

## Примечания

1. За отметку 0,000 принят уровень чистого пола. Высоты H — от чистого пола до оси изделия; привязки — от чистовой грани стены до оси механизма (у рамки на несколько постов — до оси рамки).
2. Высота установки, не указанная на плане: розетки LAN и ТВ — 300 мм от чистого пола.
3. Слаботочные кабели — отдельно от силовых: в своей трубе или лотке, при параллельной прокладке не ближе 100 мм к силовым, пересечения под прямым углом; каждую точку — отдельным кабелем от ЩС** без скруток.
4. Трассы на листе — принципиальные; фактические зафиксировать исполнительной схемой до закрытия отделкой. Силовые линии, УЗО 30 мА, ДСУП, кабель нг(A)-LS — по листам розеток и щита.
5. Проект силовой части и расчёт токов КЗ — по проекту ЭОМ; слаботочная часть согласуется с провайдером и управляющей компанией (домофон, коллективное ТВ).

1000 мм · печать 1:1

| Изм. | Кол.уч | Лист | № док. | Подп. | Дата |
|---|---|---|---|---|---|
| Разраб. | | Кырлан А.С. | | | 18.10.26 |
| Пров. | | | | | |
| ГИП | | | | | |
| | | | | | |
| Н. контр. | | | | | |
| Утв. | | | | | |

**ГД-2026-008-АИ**

Квартира с кабинетом

Общая площадь 127,29* м² · * размеры со скана, не замерены (реестр — л. 6, К-1)

Дизайн-проект интерьера

| Стадия | Лист | Листов |
|---|---|---|
| РП | 27 | 92 |

**План слаботочных сетей**

М 1:100

**Кырлан Александр Сергеевич**

выпуск 18.10.2026 · d2d5a25dca · стр. 32 из 129

04

# Отопление и вентиляция

Кырлан Александр Сергеевич

выпуск 18.10.2026 · d2d5a25dca · стр. 33 из 129

# План вентиляции

Вытяжка, приток, переток · кондиционирование не предусмотрено · размеры в мм · высоты от чистого пола

**ПРЕДВАРИТЕЛЬНО · не для производства работ · открыто пунктов: 4 (реестр — л. 6)**

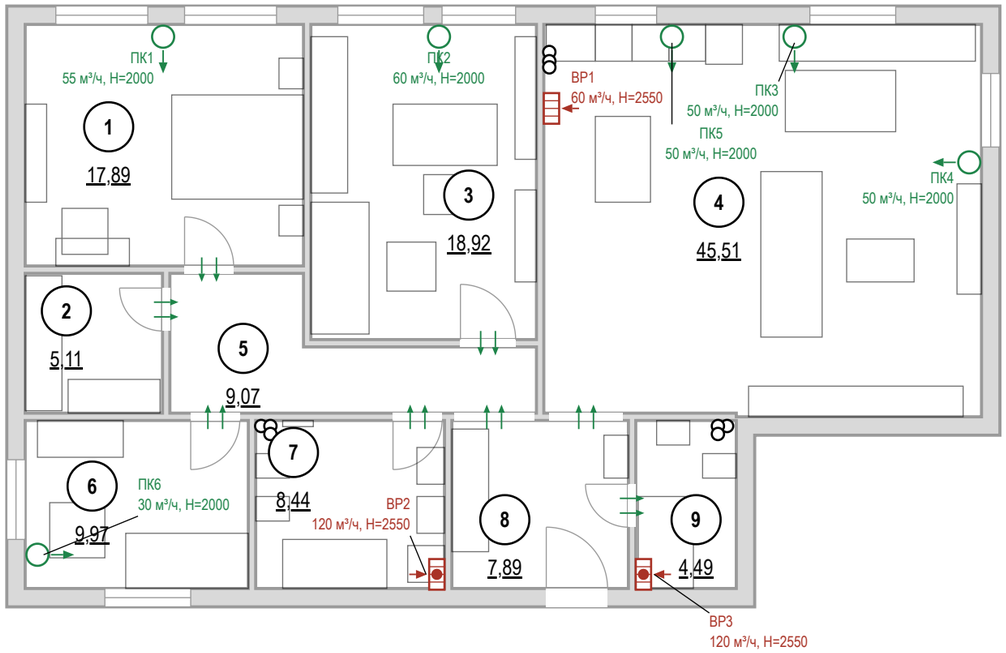


## Условные обозначения

- стояк: К1 — канализация, В1 — ХВС, Т3 — ГВС
- номер помещения, площадь м²
- вытяжная решётка в вентканал: марка, расход м³/ч, Н центра от чистого пола
- вытяжная решётка с бытовым вентилятором и обратным клапаном: марка, расход, Н
- приточный клапан (КИВ) в наружной стене: марка, расход, Н центра
- переток: зазор под полотном или переточная решётка

## Воздухообмен, м³/ч

| № | Помещение | Выт. норма | Выт. проект | Прит. норма | Прит. проект | Устройства |
|---|---|---|---|---|---|---|
| 1 | Спальня | | | 54 | 55 | ПК1 |
| 2 | Гардеробная-постирочная | 3 | | | | переток |
| 3 | Кабинет | | | 57 | 60 | ПК2 |
| 4 | Кухня-гостиная | 60 | 60 | 137 | 150 | ВР1, ПК3, ПК4, ПК5 |
| 6 | Детская | | | 30 | 30 | ПК6 |
| 7 | Ванная | 50 | 120 | | | ВР2 |
| 9 | Санузел гостевой | 50 | 120 | | | ВР3 |
| | **Итого** | **163** | **300** | **90** | **295** | |

Воздухообмен квартиры — по большей из сумм притока и вытяжки: норма 163 м³/ч, проект 300 м³/ч.
Вытяжка не меньше притока — баланс сведён.

## Примечания

1. Расчёт систем ОВ и подбор оборудования — проектная организация с допуском СРО; лист даёт места, трассы и привязки.
2. Нормы вытяжки — СП 54.13330.2022 (Изм. 1, 2), табл. 7.1: кухня с электроплитой 60 м³/ч, с газовой 100; ванная и совмещённый санузел 50; уборная 25; гардеробная 0,2 ч⁻¹. Приток в жилые — 3 м³/ч на 1 м² (менее 20 м² общей площади на человека), иначе 30 м³/ч на человека.
3. Вентканалы и шахты не сужать, не переносить и не закрывать; вентилятор и кухонная вытяжка — через обратный клапан, без перекрытия естественной тяги.
4. Проектные расходы — не ниже нормы, вытяжка сведена с притоком вентиляторами мокрых помещений. Клапаны — в простенке у окна, центр 2000 мм, не над кроватью, не ближе 300 мм к стоякам отопления; типоразмер — на расход.
5. Переток — зазор под полотнами межкомнатных дверей или переточная решётка.
6. Кондиционирование заданием не предусмотрено; при установке трассы фреона и дренажа (не менее 40 мм/м, в К1 через сифон) и питание заложить до черновых работ.
7. Привязки оборудования — по паспортам приобретённых моделей, до черновых работ.

**Допущения и предложения на листе**

Основа листа: размеры сняты с растрового плана заказчика с частичными размерами: рисунок не в масштабе, помещения выровнены по подписанным размерам мебели и проходов; контрольный обмер не выполнен (К-1); высота потолка 2700 мм принята: на плане заказчика её нет (К-2); толщины стен 300 / 120 мм приняты по плану заказчика, не замерены (К-1); разрешённая мощность 15 кВт принята по типовым ТУ для квартиры, ТУ заказчиком не переданы (К-4).
См. лист открытых вопросов (лист 6, записи К-1, К-2, К-4).

1000 мм · печать 1:1

| Изм. | Кол.уч | Лист | № док. | Подп. | Дата |
|---|---|---|---|---|---|
| Разраб. | | Кырлан А.С. | | | 18.10.26 |
| Пров. | | | | | |
| ГИП | | | | | |
| Н. контр. | | | | | |
| Утв. | | | | | |

**ГД-2026-008-АИ**

Квартира с кабинетом

Общая площадь 127,29* м² · * размеры со скана, не замерены (реестр — л. 6, К-1)

Дизайн-проект интерьера

| Стадия | Лист | Листов |
|---|---|---|
| РП | 28 | 92 |

**План вентиляции**

М 1:100

**Кырлан Александр Сергеевич**

# План отопления

Радиаторы, стояки, подводки · размеры в мм · высоты от чистого пола

**ПРЕДВАРИТЕЛЬНО · не для производства работ · открыто пунктов: 4 (реестр — л. 6)**

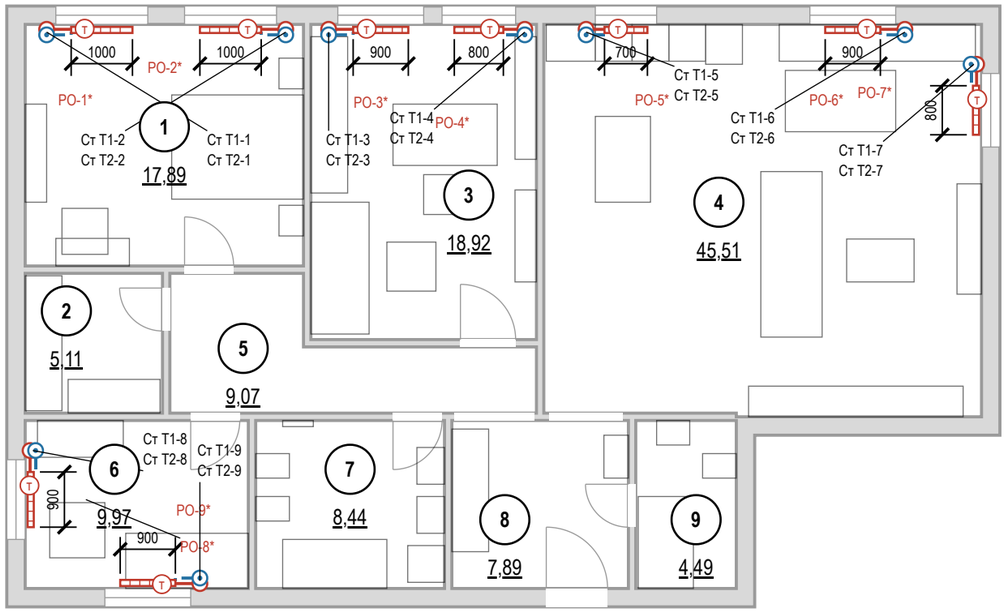


## Условные обозначения

- (1) — номер помещения, площадь м²
- радиатор отопления (марка PO-N, длина по плану)
- (T) — клапан с термоголовкой на подаче
- стояк отопления, подающий (Ст T1-N)
- стояк отопления, обратный (Ст T2-N)
- T1 — отопление, подающий трубопровод
- T2 — отопление, обратный трубопровод

## Ведомость радиаторов

| Марка | Помещение | Тип | Д×В×Г, мм | Низ / стена | Q, Вт |
|---|---|---|---|---|---|
| PO-1 | 1. Спальня | панельный* | 1000×500×100 | 120 / 40 | расч. |
| PO-2 | 1. Спальня | панельный* | 1000×500×100 | 120 / 40 | расч. |
| PO-3 | 3. Кабинет | панельный* | 900×500×100 | 120 / 40 | расч. |
| PO-4 | 3. Кабинет | панельный* | 800×500×100 | 120 / 40 | расч. |
| PO-5 | 4. Кухня-гостиная | панельный* | 700×600×100 | 120 / 40 | расч. |
| PO-6 | 4. Кухня-гостиная | панельный* | 900×600×100 | 120 / 40 | расч. |
| PO-7 | 4. Кухня-гостиная | панельный* | 800×500×100 | 120 / 40 | расч. |
| PO-8 | 6. Детская | панельный* | 900×500×100 | 120 / 40 | расч. |
| PO-9 | 6. Детская | панельный* | 900×500×100 | 120 / 40 | расч. |

* тип и мощность — по теплотехническому расчёту
Низ — от чистого пола, стена — зазор до задней панели, мм.

**Привязки — до обмера**
Стояки отопления в исходных данных не заданы: показаны у откосов окон, подводки — принципиально. До черновых работ — обмер стояков и паспорта приборов; лист перевыпустить по факту.

## Примечания

1. Расчёт системы отопления, теплопотерь и подбор приборов — проектная организация с допуском СРО; лист даёт места и привязки.
2. Тип, длина и мощность радиаторов — по теплотехническому расчёту; лист задаёт места, зазоры и подключение.
3. Радиаторы — под каждым окном жилых комнат и кухни, центр по оси проёма, длина 0,7 ширины окна (кратно 100); окончательно — по расчёту.
4. Зазоры радиатора: низ не менее 100 мм от чистого пола, верх не менее 100 мм до подоконника, 30–50 мм от стены до задней панели; центр по оси окна с допуском ±20 мм.
5. Радиаторы не закрывать глухими коробами и мебелью; перенос и замена приборов в многоквартирном доме — переустройство, согласование с управляющей организацией (ЖК РФ ст. 25–26); вынос на лоджию запрещён.
6. Трубы отопления через межквартирные стены не прокладывать (СП 51.13330.2011, п. 9.19); через перекрытия и перегородки — в гильзах.
7. Привязки приборов и подводок — по паспортам приобретённых радиаторов и клапанов, до черновых работ.
8. До закрытия отделкой трубопроводы отопления испытать гидростатическим давлением с оформлением акта (СП 73.13330.2016, 7.2–7.3).

**Допущения и предложения на листе**
Основа листа: размеры сняты с растрового плана заказчика с частичными размерами: рисунок не в масштабе, помещения выровнены по подписанным размерам мебели и проходов; контрольный обмер не выполнен (К-1); высота потолка 2700 мм принята: на плане заказчика её нет (К-2); толщины стен 300 / 120 мм приняты по плану заказчика, не замерены (К-1); разрешённая мощность 15 кВт принята по типовым ТУ для квартиры, ТУ заказчиком не переданы (К-4).
См. лист открытых вопросов (лист 6, записи К-1, К-2, К-4).

1000 мм · печать 1:1

| Изм. | Кол.уч | Лист | № док. | Подп. | Дата |
|---|---|---|---|---|---|
| Разраб. | | Кырлан А.С. | | | 18.10.26 |
| Пров. | | | | | |
| ГИП | | | | | |
| | | | | | |
| Н. контр. | | | | | |
| Утв. | | | | | |

**ГД-2026-008-АИ**

Квартира с кабинетом

Общая площадь 127,29* м² · * размеры со скана, не замерены (реестр — л. 6, К-1)

Дизайн-проект интерьера

| Стадия | Лист | Листов |
|---|---|---|
| РП | 29 | 92 |

**План отопления**

М 1:100

**Кырлан Александр Сергеевич**

05

# Водоснабжение и канализация

Кырлан Александр Сергеевич

выпуск 18.10.2026 · d2d5a25dca · стр. 36 из 129

# План выводов сантехники

Выводы В1, Т3, К1 · привязки от чистовых стен · высоты от чистого пола, мм



### Фрагмент 1. Ванная (пом. 7)

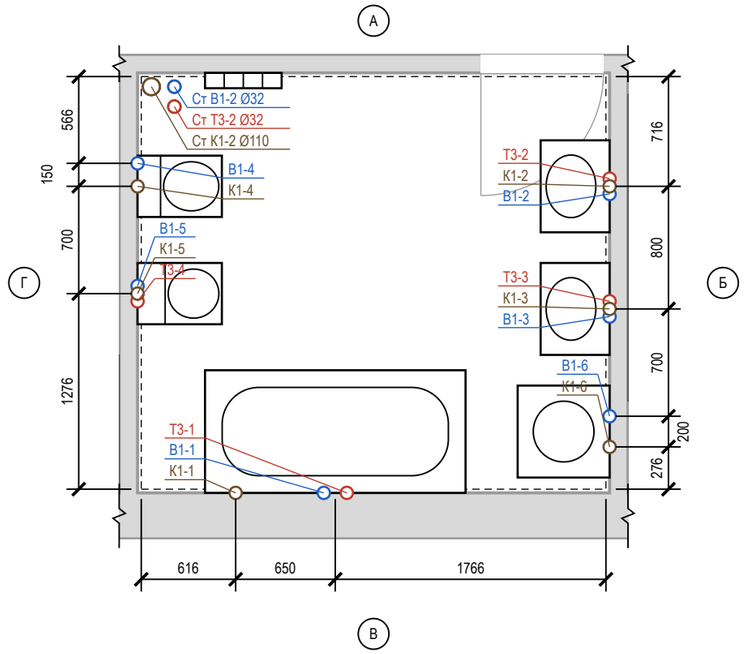


### Фрагмент 2. Санузел гостевой (пом. 9)

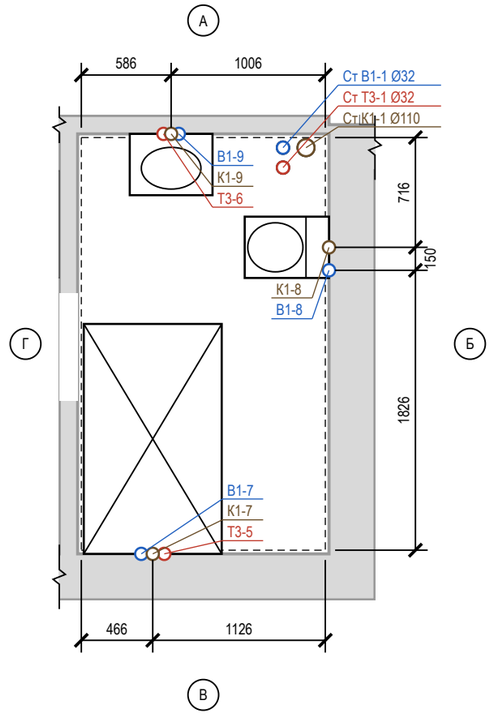


### Фрагмент 3. Кухня-гостиная (пом. 4)

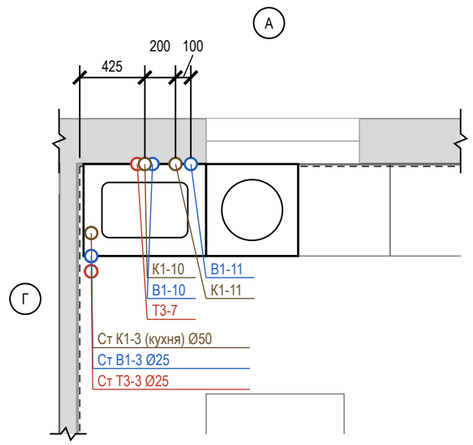


**Допущения и предложения на листе**

Основа листа: размеры сняты с растрового плана заказчика с частичными размерами: рисунок не в масштабе, помещения выровнены по подписанным размерам мебели и проходов; контрольный обмер не выполнен (К-1); высота потолка 2700 мм принята: на плане заказчика её нет (К-2); толщины стен 300 / 120 мм приняты по плану заказчика, не замерены (К-1); разрешённая мощность 15 кВт принята по типовым ТУ для квартиры, ТУ заказчиком не переданы (К-4).

См. лист открытых вопросов (лист 6, записи К-1, К-2, К-4).

### Условные обозначения

- вывод В1 (код — в ведомости привязок)
- вывод Т3 (код — в ведомости привязок)
- вывод К1 (код — в ведомости привязок)
- сантехприбор по расстановке (габарит модели)
- чистовая поверхность стены (от неё привязки)
- стояк «Ст К1-N / Ст В1-N» (ГОСТ 21.601), Ø мм
- линия обрыва (граница фрагмента)
- А — обозначение стены А–Г (как на развёртках)

### Ведомость привязок выводов

| Код | Прибор | Ø | Н, мм | Привязка от чист. стен, мм | Прим. |
|---|---|---|---|---|---|
| В1-1 | П1 ванна | ½" | 200 | ст. В: 1191 от Г | межос. 150 |
| Т3-1 | П1 ванна | ½" | 200 | ст. В: 1341 от Г | межос. 150 |
| К1-1 | П1 ванна | Ø50 | 50 | ст. В: 616 от Г | |
| В1-2 | П2 умывальник | ½" | 550 | ст. Б: 766 от А | межос. 100 |
| Т3-2 | П2 умывальник | ½" | 550 | ст. Б: 666 от А | межос. 100 |
| К1-2 | П2 умывальник | Ø50 | 500 | ст. Б: 716 от А | |
| В1-3 | П3 умывальник | ½" | 550 | ст. Б: 1126 от В | межос. 100 |
| Т3-3 | П3 умывальник | ½" | 550 | ст. Б: 1226 от В | межос. 100 |
| К1-3 | П3 умывальник | Ø50 | 500 | ст. Б: 1176 от В | |
| В1-4 | П4 унитаз подвесной | ½" | 1000 | ст. Г: 566 от А | в раме инсталляции |
| К1-4 | П4 унитаз подвесной | Ø110 | 220 | ст. Г: 716 от А | |
| В1-5 | П5 биде | ½" | 200 | ст. Г: 1326 от В | межос. 100 |
| Т3-4 | П5 биде | ½" | 200 | ст. Г: 1226 от В | межос. 100 |
| К1-5 | П5 биде | Ø50 | 200 | ст. Г: 1276 от В | |
| В1-6 | П6 стиральная машина | ½" | 800 | ст. Б: 476 от В | кран машины |
| К1-6 | П6 стиральная машина | Ø50 | 600 | ст. Б: 276 от В | |
| В1-7 | П10 душ | ½" | 1000 | ст. В: 391 от Г | межос. 150 |
| Т3-5 | П10 душ | ½" | 1000 | ст. В: 541 от Г | межос. 150 |
| К1-7 | П10 душ | Ø50 | 0 | ст. В: 466 от Г | сифон поддона |
| В1-8 | П11 унитаз подвесной | ½" | 1000 | ст. Б: 866 от А | в раме инсталляции |
| К1-8 | П11 унитаз подвесной | Ø110 | 220 | ст. Б: 716 от А | |
| В1-9 | П12 умывальник | ½" | 550 | ст. А: 636 от Г | межос. 100 |
| Т3-6 | П12 умывальник | ½" | 550 | ст. А: 536 от Г | межос. 100 |
| К1-9 | П12 умывальник | Ø50 | 500 | ст. А: 586 от Г | |
| В1-10 | П13 мойка кухонная | ½" | 600* | ст. А: 475 от Г | межос. 100 |
| Т3-7 | П13 мойка кухонная | ½" | 600* | ст. А: 375 от Г | межос. 100 |
| К1-10 | П13 мойка кухонная | Ø50 | 400* | ст. А: 425 от Г | |
| В1-11 | П14 посудомоечная машина | ½" | 550* | ст. А: 725 от Г | кран ПММ в шкафу мойки |
| К1-11 | П14 посудомоечная машина | Ø40 | 550* | ст. А: 625 от Г | слив ПММ в шкафу мойки |

* — высота по практике монтажа; сверить по паспорту прибора

### Примечания

1. Привязки выводов даны от чистовых поверхностей стен (облицовка на сторону: ванная — 24 мм (штукатурка 10 + клей 5 + плитка 9); санузел гостевой 24 мм (штукатурка 10 + клей 5 + плитка 9); кухня-гостиная — 24 мм (фартук: штукатурка 10 + клей 5 + плитка 9)); эти же грани — на развёртках и в раскладке плитки. Высоты — от чистого пола помещения.
2. Высоты и межосевые, отмеченные «*», приняты по практике монтажа; до черновой разводки сверить по паспорту выбранного прибора (смеситель, инсталляция, сифон).
3. Горячая вода (Т3) — слева от холодной (В1), если смотреть на прибор. Допуск установки выводов: ±5 мм в группе, ±20 мм у отдельно стоящих.
4. Расчёт систем водоснабжения и канализации и подбор оборудования выполняет проектная организация; лист задаёт места и высоты выводов.
5. Посудомоечная машина П14: кран и слив — отдельными выводами в шкафу мойки (не за машиной), до машины ≤ 1500 мм.
6. Прибор П13 мойка кухонная, П14 посудомоечная машина взят из расстановки мебели (по шкафу с мойкой).

1000 мм · печать 1:1

| Изм. | Кол.уч | Лист | № док. | Подп. | Дата |
|---|---|---|---|---|---|
| Разраб. | | Кырлан А.С. | | | 18.10.26 |
| Пров. | | | | | |
| ГИП | | | | | |
| | | | | | |
| Н. контр. | | | | | |
| Утв. | | | | | |

**ГД-2026-008-АИ**

Квартира с кабинетом

Общая площадь 127,29* м² · * размеры со скана, не замерены (реестр — л. 6, К-1)

Дизайн-проект интерьера

| Стадия | Лист | Листов |
|---|---|---|
| РП | 30 | 92 |

**План выводов сантехники**

М 1:40

**Кырлан Александр Сергеевич**

выпуск 18.10.2026 № d2d5a25dca · стр. 37 из 129

# Схема разводки водопровода и канализации

Схемы систем В1, Т3, К1 · трассы принципиальные · уклоны в мм на 1 м · план М 1:400, фрагменты М 1:40

**ПРЕДВАРИТЕЛЬНО · не для производства работ · открыто пунктов: 4 (реестр — л. 6)**

## План квартиры (М 1:400)

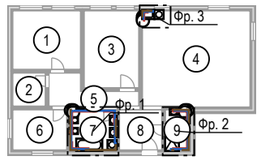


## Фр. 1. Ванная (М 1:40)

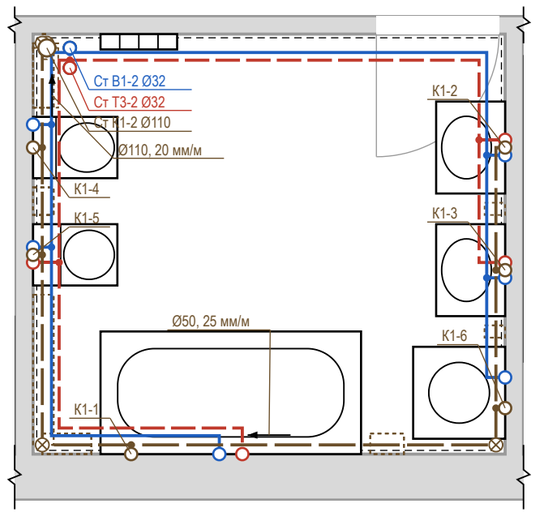


## Фр. 2. Санузел гостевой (М 1:40)

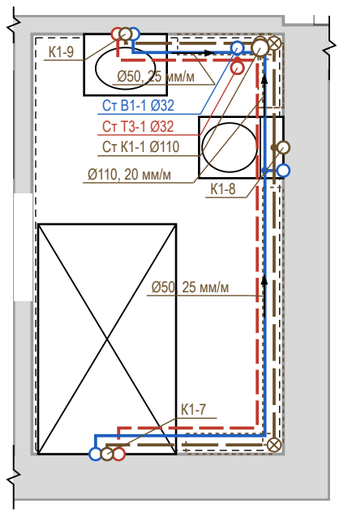


## Фр. 3. Кухня-гостиная (М 1:40)

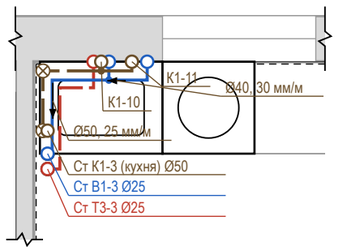


## Узел ввода В1, Т3 (схема, без масштаба)

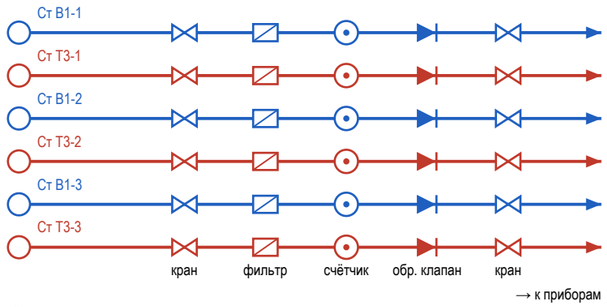


⊗ Ст К1-1, Ст К1-2, Ст К1-3 (кухня): ревизия на стояке — люк в коробе

## Условные обозначения

- В1 — водопровод хозяйственно-питьевой (ХВС), PP-R Ø20
- Т3 — горячее водоснабжение, подача (ГВС), PP-R Ø20
- К1 — канализация бытовая
- направление уклона К1 / пола: Ø, мм на 1 м
- ⊗ ревизия (прочистка) К1 — доступ сохранить
- • тройник (ответвление к прибору)
- короб К1 над чистым полом (ГКЛВ под плитку)
- ○ вывод В1 (код — в ведомости привязок)
- ○ вывод Т3 (код — в ведомости привязок)
- ○ вывод К1 (код — в ведомости привязок)
- сантехприбор по расстановке (габарит модели)
- ○ стояк «Ст К1-N / Ст В1-N» (ГОСТ 21.601), Ø мм
- линия обрыва (граница фрагмента)
- граница фрагмента на плане (Фр. N)

## Профиль выпусков К1 (до врезки в стояк)

| Выпуск | Прибор | Ø | L, м | i, мм/м | Δh, мм | Прокладка, мм |
|---|---|---|---|---|---|---|
| К1-8 | П11 унитаз подвесной | Ø110 | 0,86 | 20 | 17 | короб 160×140 |
| К1-4 | П4 унитаз подвесной | Ø110 | 0,80 | 20 | 16 | короб 160×140 |
| К1-2 | П2 умывальник | Ø50 | 7,64 | 25 | 191 | короб 280×110 |
| К1-3 | П3 умывальник | Ø50 | 6,84 | 25 | 171 | короб 260×110 |
| К1-6 | П6 стиральная машина | Ø50 | 5,94 | 25 | 149 | короб 230×110 |
| К1-7 | П10 душ | Ø50 | 3,89 | 25 | 97 | короб 180×110 |
| К1-1 | П1 ванна | Ø50 | 3,32 | 25 | 83 | короб 170×110 |
| К1-5 | П5 биде | Ø50 | 1,50 | 25 | 38 | короб 120×110 |
| К1-9 | П12 умывальник | Ø50 | 0,97 | 25 | 24 | короб 110×110 |
| К1-10 | П13 мойка кухонная | Ø50 | 0,86 | 25 | 22 | над полом за приборами |
| К1-11 | П14 посудомоечная машина | Ø40 | 1,06 | 30 | 32 | над полом за приборами |

Короб h×b: h — от чистого пола, b — от чистовой стены. Стяжка 35 мм — лист полов.

## Примечания

1. Трассы принципиальные, построены от стояков вдоль стен помещений; фактическое положение фиксируется исполнительной схемой с привязками (фото с рулеткой) до закрытия.
2. Уклон К1 не менее 1/d и не более 150 мм/м (СП 30.13330.2020, п. 19.1), приняты практические уклоны; поворот — двумя отводами 45°, ревизия после поворота, доступ сохранить. Стояк К1 в коробе — звукоизоляция стояка в коробе, без жёсткого контакта короба с трубой.
3. Решение по К1: стяжка 35 мм не укрывает трубы (нужно Ø + Δh + 45 мм) — выпуски идут над чистым полом вдоль стен: К1-10, К1-11 — за приборами и в раме инсталляции; К1-8, К1-4, К1-2, К1-3, К1-6, К1-7, К1-1, К1-5, К1-9 — в коробе ГКЛВ под плитку (размеры в профиле). Короба — на развёртках; отметку низа врезки в стояк замерить до черновых работ.
4. На каждом вводе В1 и Т3 — кран шаровой, фильтр, счётчик, обратный клапан; доступ через люк не меньше 300×400. Водопровод — в штробе стен или в коробах; трубы испытать давлением до закрытия (акт скрытых работ).
5. Расчёт систем, диаметры магистралей и подбор оборудования выполняет проектная организация; врезка и перенос стояков — по согласованию с управляющей организацией. Арматуру и привязки сверить по паспортам приборов.

**Допущения и предложения на листе**

Основа листа: размеры сняты с растрового плана заказчика с частичными размерами: рисунок не в масштабе, помещения выровнены по подписанным размерам мебели и проходов; контрольный обмер не выполнен (К-1); высота потолка 2700 мм принята: на плане заказчика её нет (К-2); толщины стен 300 / 120 мм приняты по плану заказчика, не замерены (К-1); разрешённая мощность 15 кВт принята по типовым ТУ для квартиры, ТУ заказчиком не переданы (К-4).
См. лист открытых вопросов (лист 6, записи К-1, К-2, К-4).

| Изм. | Кол.уч | Лист | № док. | Подп. | Дата |
|---|---|---|---|---|---|
| Разраб. | | Кырлан А.С. | | | 18.10.26 |
| Пров. | | | | | |
| ГИП | | | | | |
| | | | | | |
| Н. контр. | | | | | |
| Утв. | | | | | |

**ГД-2026-008-АИ**

Квартира с кабинетом

Общая площадь 127,29* м² · * размеры со скана, не замерены (реестр — л. 6, К-1)

Дизайн-проект интерьера

| Стадия | Лист | Листов |
|---|---|---|
| РП | 31 | 92 |

**Схема разводки водопровода и канализации**

М б/м

**Кырлан Александр Сергеевич**

выпуск 18.10.2026 № d2d5a25dca · стр. 38 из 129

# Спецификация сантехнического оборудования

**ПРЕДВАРИТЕЛЬНО · не для производства работ · открыто пунктов: 4 (реестр — л. 6)**

Форма 1 ГОСТ 21.110-2013 · ГД-2026-008-АИ-ВК.СО · приборы, арматура, трубопроводы

| Поз. | Наименование и техническая характеристика | Тип, марка, обозначение документа | Код продукции | Поставщик | Ед. изм. | Кол. | Масса 1 ед., кг | Примечание |
|---|---|---|---|---|---|---|---|---|
| | Санитарные приборы | | | | | | | |
| 1 | Ванна акриловая 1700×800 мм, с каркасом, экраном и отверстием слив-перелив | ванна отдельностоящая овальная 1700×800, литой камень; смеситель напольный | | выбор заказчика | шт | 1 | | П1 |
| 2 | Унитаз подвесной безободковый, с сиденьем микролифт, крепёж и звукоизолирующая прокладка | Jacob Delafon Struktura EDF102-00 | | выбор заказчика | шт | 2 | | П4, П11 |
| 3 | Инсталляция для подвесного унитаза: рама высотой 1120 мм, бачок, клавиша смыва (ось клавиши 1050 мм от чистого пола) | аналог | | выбор заказчика | шт | 2 | | П4, П11; короб ГКЛВ |
| 4 | Умывальник подвесной 600×450 мм, с отверстием под смеситель и переливом | раковина накладная овальная на тумбе 1500 (1 из 2) | | выбор заказчика | шт | 2 | | П2, П3 |
| 5 | Умывальник подвесной 540×400 мм, с отверстием под смеситель и переливом | раковина 540 на консоли, травертин | | выбор заказчика | шт | 1 | | П12 |
| 6 | Биде подвесное | аналог | | выбор заказчика | шт | 1 | | П5 |
| 7 | Поддон душевой низкий 900×1500 мм, с сифоном и выпуском Ø50, на ножках/подиуме | душ с трапом и стеклянной перегородкой | | выбор заказчика | шт | 1 | | П10 |
| 8 | Мойка кухонная 800×600 мм, с переливом | аналог | | с кухонной мебелью | шт | 1 | | П13 |
| 9 | Полотенцесушитель электрический, IP44, с терморегулятором | аналог | | выбор заказчика | шт | 1 | | П7 |
| | Смесители, сифоны и арматура приборов | | | | | | | |
| 10 | Смеситель для ванны настенный однорычажный, межосевое 150 мм, с душевым набором (лейка, шланг, держатель) | аналог | | выбор заказчика | шт | 1 | | П1 |
| 11 | Смеситель для умывальника однорычажный, с донным клапаном | аналог | | выбор заказчика | шт | 3 | | П2, П3, П12 |
| 12 | Душевая система скрытого монтажа с термостатом: встраиваемая часть, верхний душ, ручная лейка | аналог | | выбор заказчика | шт | 1 | | П10; встраиваемая часть — до плитки |
| 13 | Смеситель кухонный однорычажный, высокий излив | аналог | | выбор заказчика | шт | 1 | | П13 |
| 14 | Обвязка ванны слив-перелив Ø40/50 с сифоном | аналог | | выбор заказчика | шт | 1 | | П1 |
| 15 | Сифон для умывальника бутылочный Ø32/40–50, с гофрой к выпуску | аналог | | выбор заказчика | шт | 3 | | П2, П3, П12 |
| 16 | Сифон для мойки с отводом для ПММ Ø40/50 | аналог | | выбор заказчика | шт | 1 | | П13 |
| 17 | Сифон для стиральной машины встраиваемый в стену Ø50, с обратным клапаном | аналог | | выбор заказчика | шт | 1 | | П6 |
| 18 | Кран угловой ½"×½" с гибкой подводкой 40 см (умывальники, мойка) | аналог | | выбор заказчика | шт | 8 | | по 2 на прибор |
| 19 | Кран шаровой угловой ½"×¾" для подключения стиральной и посудомоечной машины | аналог | | выбор заказчика | шт | 2 | | П6, П14 |
| | Трубопроводы | | | | | | | |
| 20 | Труба полипропиленовая PP-R PN20 Ø20×3,4 (В1) | ГОСТ 32415-2013 | | выбор заказчика | м | 25 | 0,17 | 15,5 + 7,0 + 10 % |
| 21 | Труба PP-R, армированная стекловолокном, PN20 Ø20×2,8 (Т3) | ГОСТ 32415-2013 | | выбор заказчика | м | 19,5 | 0,15 | 14,0 + 3,6 + 10 % |
| 22 | Труба канализационная ПП Ø40 (К1) | ГОСТ 32414-2013 | | выбор заказчика | м | 1 | | 0,3 + 0,6 + 10 % |
| 23 | Труба канализационная ПП Ø50 (К1) | ГОСТ 32414-2013 | | выбор заказчика | м | 16,5 | | 12,0 + 2,8 + 10 % |
| 24 | Труба канализационная ПП Ø110 (К1) | ГОСТ 32414-2013 | | выбор заказчика | м | 2,5 | | 1,7 + 0,4 + 10 % |
| | Фасонные части и выводы | | | | | | | |
| 25 | Отвод канализационный ПП 45° Ø40 | ГОСТ 32414-2013 | | выбор заказчика | шт | 2 | | 2 шт. на поворот |
| 26 | Отвод канализационный ПП 45° Ø50 | ГОСТ 32414-2013 | | выбор заказчика | шт | 18 | | 2 шт. на поворот |
| 27 | Отвод канализационный ПП 45° Ø110 | ГОСТ 32414-2013 | | выбор заказчика | шт | 12 | | 2 шт. на поворот |
| 28 | Тройник канализационный ПП 45° (врезки ветвей) | ГОСТ 32414-2013 | | выбор заказчика | шт | 10 | | |
| 29 | Ревизия канализационная ПП (после поворота трассы) | ГОСТ 32414-2013 | | выбор заказчика | шт | 9 | | доступ сохранить |
| 30 | Фитинги PP-R Ø20: тройники, угольники 90° (ветви и повороты В1, Т3) | ГОСТ 32415-2013 | | выбор заказчика | шт | 44 | | |
| 31 | Водорозетка PP-R Ø20×½" настенная, с креплением | ГОСТ 32415-2013 | | выбор заказчика | шт | 18 | | коды — лист выводов |
| | Узлы ввода, люки, короба | | | | | | | |
| 32 | Кран шаровой латунный Ду15 PN16 (отключение ввода) | аналог | | выбор заказчика | шт | 6 | | Ст В1-1, Ст Т3-1, Ст В1-2, Ст Т3-2, Ст В1-3, Ст Т3-3 |
| 33 | Фильтр сетчатый косой Ду15 | аналог | | выбор заказчика | шт | 6 | | |
| 34 | Счётчик воды крыльчатый Ду15 (ХВ, ГВ), с поверкой | аналог | | выбор заказчика | шт | 6 | | пломба УК |
| 35 | Клапан обратный Ду15 | аналог | | выбор заказчика | шт | 6 | | |
| 36 | Люк ревизионный нажимной под плитку 300×400 мм | аналог | | выбор заказчика | шт | 2 | | к стоякам и арматуре |
| 37 | Звукоизоляция стояка К1 в коробе: рулонный звукоизоляционный материал ≥ 10 мм, обмотка стояка на высоту этажа | аналог | | выбор заказчика | м | 8,1 | | Ст К1-1, Ст К1-2, Ст К1-3 (кухня) |
| 38 | Короб К1 над полом: профиль ПН/ПС, ГКЛВ 12,5 мм под плитку | аналог | | выбор заказчика | м | 15,2 | | сечение — лист разводки |

## Примечания

1. Форма 1 ГОСТ 21.110-2013, ширины граф изменены по п. 4.1. «Аналог» — аналог по характеристикам: модели внести до черновых работ, привязки выводов сверить по паспортам.
2. Бытовая техника не входит (показана арматура подключения), мойка — в комплекте кухни. Длины труб — трасса листа разводки + подъёмы + 10 %.
3. Стояк К1 в коробе — звукоизоляция стояка в коробе без жёсткого контакта короба с трубой.
4. Расчёт систем водоснабжения и канализации, диаметры магистралей и подбор оборудования выполняет проектная организация.

**Допущения и предложения на листе**

Основа листа: размеры сняты с растрового плана заказчика с частичными размерами: рисунок не в масштабе, помещения выровнены по подписанным размерам мебели и проходов; контрольный обмер не выполнен (К-1); высота потолка 2700 мм принята: на плане заказчика её нет (К-2); толщины стен 300 / 120 мм приняты по плану заказчика, не замерены (К-1); разрешённая мощность 15 кВт принята по типовым ТУ для квартиры, ТУ заказчиком не переданы (К-4).

См. лист открытых вопросов (лист 6, записи К-1, К-2, К-4).

| Изм. | Кол.уч | Лист | № док. | Подп. | Дата |
|---|---|---|---|---|---|
| | | | | | |
| | | | | | |
| | | | | | |
| | | | | | |

**ГД-2026-008-АИ**

Квартира с кабинетом

Общая площадь 127,29* м² · * размеры со скана, не замерены (реестр — л. 6, К-1)

| | | | |
|---|---|---|---|
| Разраб. | Кырлан А.С. | | 18.10.26 |
| Пров. | | | |
| ГИП | | | |
| | | | |
| Н. контр. | | | |
| Утв. | | | |

Дизайн-проект интерьера

| Стадия | Лист | Листов |
|---|---|---|
| РП | 32 | 92 |

**Спецификация сантехнического оборудования**

М б/м

**Кырлан Александр Сергеевич**

выпуск 18.10.2026 № d2d5a25dca · стр. 39 из 129

# Спецификация светильников и сценарии освещения

Светильники, ленты и блоки питания, слои света и сценарии по помещениям · б/м

## Спецификация светильников

| Поз. | Марки | Наименование | Установка | Кол. | P, Вт | Σ P, Вт | Ф, лм | Тц, К | Ra | Угол, ° | IP | Дим. | Группа | Пом. |
|---|---|---|---|---|---|---|---|---|---|---|---|---|---|---|
| 1 | Св1–Св8 | Встраиваемый точечный | встраиваемый | 8 | 12 | 96 | 1000 | 2700 | 90 | — | 20 | — | L1 | 1 |
| 2 | Св9 | Лента светодиодная 24 В | в коробе, профиль с рассеивателем | 15,5 м | 9,6/м | 148,8 | 900/м | 2700 | 90 | — | 20 | да | L2 | 1 |
| 3 | Св10, Св11, Св24, Св25 | Настенный (бра) | на стене, H=1500 | 6 | 6 | 36 | 400 | 2700 | 90 | 60 | 20 | — | L3, L9 | 1, 3, 6 |
| 4 | Св16 | Потолочный накладной | на потолке, засветка стены | 1 | 10 | 10 | 900 | 3000 | 90 | — | 20 | — | L6 | 2 |
| 5 | Св17–Св22 | Встраиваемый точечный | встраиваемый | 12 | 12 | 144 | 1050 | 2700 | 90 | — | 20 | — | L7 | 3, 6 |
| 6 | Св23 | Лента светодиодная 24 В | в коробе, профиль с рассеивателем | 24,6 м | 9,6/м | 236,2 | 900/м | 2700 | 90 | — | 20 | да | L8 | 3, 6 |
| 7 | Св31–Св40 | Встраиваемый точечный | встраиваемый | 10 | 12 | 120 | 1000 | 3000 | 90 | — | 20 | да | L12 | 4 |
| 8 | Св41 | Лента светодиодная 24 В | в коробе, профиль с рассеивателем | 22,1 м | 9,6/м | 212,2 | 900/м | 2700 | 90 | — | 20 | да | L13 | 4 |
| 9 | Св42**, Св43**, Св44** | Подвесной | подвес, низ H=1450 | 3 | 9 | 27 | 800 | 3000 | 90 | — | 20 | да | L14 | 4 |
| 10 | Св45–Св48 | Встраиваемый точечный | встраиваемый | 4 | 10 | 40 | 900 | 3000 | 90 | — | 20 | да | L15 | 4 |
| 11 | Св49** | Линейный настенный | под верхними шкафами, H=1440 | 1 | 18 | 18 | 1500 | 3000 | 90 | — | 20 | да | L16 | 4 |
| 12 | Св26–Св29, Св53, Св54 | Встраиваемый точечный | встраиваемый | 6 | 7 | 42 | 600 | 3000 | 90 | — | 20 | — | L10 | 5, 8 |
| 13 | Св12–Св14, Св51 | Встраиваемый точечный | встраиваемый | 4 | 6 | 24 | 500 | 3000 | 90 | — | 44 | — | L4, L17 | 7, 9 |
| 14 | Св15, Св52 | Настенный светильник над зеркалом, драйвер встроен | над зеркалом, H=1900 | 2 | 8 | 16 | 600 | 3000 | 90 | — | 44 | — | L5, L18 | 7, 9 |
| 15 | Св30 | Лента светодиодная 24 В | в коробе, профиль с рассеивателем, датчик движения | 1,8 м | 4,8/м | 8,6 | 150/м | 2700 | 90 | — | 20 | нет | L11 | 8 |
| 16 | Св50 | Встраиваемый точечный | встраиваемый | 1 | 7 | 7 | 600 | 3000 | 90 | — | 44 | — | L17 | 9 |
| | | **Итого** | | **58 шт + 64 м** | | **1185,8** | | | | | | | | |

## Слои света по помещениям

| Пом. | Помещение | Слои света и группы включения (марки светильников) | Тц, К | Ra | Σ P, Вт | Сцен. |
|---|---|---|---|---|---|---|
| 1 | Спальня | общий — L1 (Св1–Св8); рабочий — L3 (Св10, Св11); акцентный — L2 (Св9) | 2700 | 90 | 256,8 | 2 |
| 2 | Гардеробная-постирочная | общий — L6 (Св16) | 3000 | 90 | 10 | — |
| 3 | Кабинет | общий — L7 (Св17–Св22); рабочий — L9 (Св24, Св25); акцентный — L8 (Св23) | 2700 | 90 | 202,1 | 1 |
| 4 | Кухня-гостиная | общий — L12 (Св31–Св40), L14 (Св42**, Св43**, Св44**), L15 (Св45–Св48); рабочий — L16 (Св49**); акцентный — L13 (Св41) | 2700 / 3000 | 90 | 417,2 | 4 |
| 5 | Коридор | общий — L10 (Св53, Св54) | 3000 | 90 | 14 | — |
| 6 | Детская | общий — L7 (Св17–Св22); рабочий — L9 (Св24, Св25); акцентный — L8 (Св23) | 2700 | 90 | 202,1 | 1 |
| 7 | Ванная | общий — L4 (Св12–Св14); рабочий — L5 (Св15) | 3000 | 90 | 26 | — |
| 8 | Прихожая | общий — L10 (Св26–Св29); ночной — L11 (Св30) | 2700 / 3000 | 90 | 36,6 | — |
| 9 | Санузел гостевой | общий — L17 (Св50, Св51); рабочий — L18 (Св52) | 3000 | 90 | 21 | — |

## LED-ленты, линейные светильники и блоки питания

| Марка | Пом. | L, м | U, В | Вт/м | Σ P, Вт | БП | P БП, Вт | Загр., % | Питание | Доступ к БП |
|---|---|---|---|---|---|---|---|---|---|---|
| Св9 | 1 | 15,5 | 24 | 9,6 | 148,8 | БП1 | 200 | 74 | с двух концов | люк 300×300 в коробе У1 у входа |
| Св23 | 3 | 12,3 | 24 | 9,6 | 118,1 | БП2 | 200 | 118 | с двух концов | люк 300×300 в коробе У1 у окна |
| Св41 | 4 | 22,1 | 24 | 9,6 | 212,2 | БП4 | 300 | 71 | с двух концов | люк 300×300 в коробе У1 у входа |
| Св49** | 4 | 3 | 24 | — | 18 | БП5** | 60 | 30 | встроенный ввод | в пенале М6, верх, съёмная панель |
| Св23 | 6 | 12,3 | 24 | 9,6 | 118,1 | БП2 | 200 | 118 | с двух концов | люк 300×300 в коробе У1 у окна |
| Св30 | 8 | 1,8 | 24 | 4,8 | 8,6 | БП3 | 20 | 43 | с одного конца | в шкафу М16, верхняя полка |

## Сценарии освещения

| Пом. | Сценарий | Группы и уровни, % | Чем включается |
|---|---|---|---|
| 1 | Вечер | L1 споты — 0; L2 подсветка короба — 100; L3 бра — 100 | S1, S2, S3 |
| 1 | Уборка | L1 споты — 100; L2 подсветка короба — 100; L3 бра — 0 | S1, S2, S3 |
| 3 | Вечер | L7 споты — 0; L8 подсветка короба — 100; L9 бра — 100 | S4, S5, S6 |
| 4 | Вечер | L12 споты гостиной — 30; L13 подсветка короба — 100; L14 подвесы над столом — 50; L15 споты кухни — 0; L16 подсветка столешницы — 0 | S10 светорегулятор, S11** светорегулятор |
| 4 | Ужин | L12 споты гостиной — 0; L13 подсветка короба — 60; L14 подвесы над столом — 100; L15 споты кухни — 0; L16 подсветка столешницы — 30 | S10 светорегулятор, S11** светорегулятор, S12** светорегулятор |
| 4 | Кино | L12 споты гостиной — 0; L13 подсветка короба — 20; L14 подвесы над столом — 0; L15 споты кухни — 0; L16 подсветка столешницы — 0 | S10 светорегулятор |
| 4 | Готовка | L12 споты гостиной — 50; L13 подсветка короба — 0; L14 подвесы над столом — 0; L15 споты кухни — 100; L16 подсветка столешницы — 100 | S10 светорегулятор, S11** светорегулятор, S12** светорегулятор |
| 6 | Вечер | L7 споты — 0; L8 подсветка короба — 100; L9 бра — 100 | S4, S5, S6 |

## Слои света

общий — равномерный свет помещения, по норме освещённости

рабочий — местный свет задачи: столешница, зеркало, чтение у кровати

акцентный — подсветка потолка, стен и ниш; не входит в поток общего света

ночной — путь спальня → санузел: не выше 2700 К, малая яркость, датчик движения

## Примечания

1. Позиции и марки Св — те же, что на плане освещения (лист 21) и в ведомости светильников (лист 23); группы L — по плану выключателей (лист 22).
2. Модели светильников не назначены: подбор по графам спецификации — поток, Тц, Ra, угол, IP и диммирование не хуже указанных, мощность не больше. IP 20 — сухие помещения.
3. Длина LED-ленты в карнизе — по линии карниза плана потолков (лист 34); Σ P = Вт/м × длина. Блок питания загружен не больше чем на 80 %; лента 24 В длиннее 10 м питается с двух концов; доступ к блоку питания — люк ревизии 300×300 мм или место, указанное в таблице.
4. Сценарии: уровень — доля максимальной яркости группы, %; 0 — группа выключена. Уровень ниже 100 % — только у групп на светорегуляторе (задний фронт, ТЕ) с диммируемыми драйверами и блоками питания.
5. Мощность и поток — по паспортам принятых изделий, Σ P — установленная мощность освещения. Оценка освещённости — на плане освещения; это не светотехнический расчёт.

Допущения и предложения на листе. Основа листа: размеры сняты с растрового плана заказчика с частичными размерами: рисунок не в масштабе, помещения выровнены по подписанным размерам мебели и проходов; контрольный обмер не выполнен (К-1); высота потолка 2700 мм принята: на плане заказчика её нет (К-2); толщины стен 300 / 120 мм приняты по плану заказчика, не замерены (К-1); разрешённая мощность 15 кВт принята по типовым ТУ для квартиры, ТУ заказчиком не переданы (К-4). Знак «**» — предложение проектировщика, заказчиком не утверждено (согласовать с заказчиком): записи в реестре нет: S11, S12 — светорегулятор добавлен разработчиком проекта; Св42, Св43, Св44, Св49, БП5 — диммируемость добавлена разработчиком проекта под светорегуляторы S11 и S12. См. лист открытых вопросов (лист 6, записи К-1, К-2, К-4).

| Изм. | Кол.уч | Лист | № док. | Подп. | Дата |
|---|---|---|---|---|---|
| Разраб. | | Кырлан А.С. | | | 18.10.26 |
| Пров. | | | | | |
| ГИП | | | | | |
| | | | | | |
| Н. контр. | | | | | |
| Утв. | | | | | |

**ГД-2026-008-АИ**

Квартира с кабинетом

Общая площадь 127,29* м² · * размеры со скана, не замерены (реестр — л. 6, К-1)

Дизайн-проект интерьера

| Стадия | Лист | Листов |
|---|---|---|
| РП | 33 | 92 |

**Спецификация светильников и сценарии освещения**

М б/м

**Кырлан Александр Сергеевич**

06

# Потолки и ГКЛ-конструкции

Кырлан Александр Сергеевич

выпуск 18.10.2026 · d2d5a25dca · стр. 41 из 129

# План потолков

Уровни и марки потолков, короба с подсветкой, ниши под шторы, люки, вырезы · отметки низа от ±0,000 чистого пола · размеры в мм

**ПРЕДВАРИТЕЛЬНО · не для производства работ · открыто пунктов: 4 (реестр — л. 6)**

## Ведомость потолков

| Пом. | Марка | Конструкция | Низ | S, м² | Q |
|---|---|---|---|---|---|
| 1 | | по плите, окраска | +2,700 | 17,89 | |
| 2 | | по плите, окраска | +2,700 | 5,11 | |
| 3 | | по плите, окраска | +2,700 | 18,92 | |
| 4 | | по плите, окраска | +2,700 | 45,51 | |
| 5 | | по плите, окраска | +2,700 | 9,07 | |
| 6 | | по плите, окраска | +2,700 | 9,97 | |
| 7 | | по плите, окраска | +2,700 | 8,44 | |
| 8 | | по плите, окраска | +2,700 | 7,89 | |
| 9 | | по плите, окраска | +2,700 | 4,49 | |
| | | **Итого** | | **127,29** | |

## Ведомость вырезов и закладных в потолке

| Марка | Устройство | Кол. | Пом. |
|---|---|---|---|
| | Светильник встраиваемый (марки — план освещения) | 45 | 1, 3, 4, 5, 6, 7, 8, 9 |
| | Светильник накладной (марки — план освещения) | 1 | 2 |
| | Светильник подвесной (марки — план освещения) | 3 | 4 |
| ИП1, ИП2, ИП4, ИП2 | Извещатель дымовой | 4 | 1, 3, 4, 6 |
| ИП5, ИП6, ИП3 | Извещатель тепловой | 3 | 4, 5, 8 |
| AP2**, AP1** | Точка доступа Wi-Fi, PoE | 2 | 4, 8 |

## Условные обозначения

- потолок по плите перекрытия, окраска, низ +2,700
- светильник встраиваемый — подложка с плана освещения
- светильник накладной — подложка с плана освещения
- светильник подвесной — подложка с плана освещения
- Д — извещатель дымовой на потолке — подложка
- Т° — извещатель тепловой на потолке — подложка
- Wi — точка доступа Wi-Fi на потолке — подложка
- +2,6 — отметка низа потолка, м; под ней марка потолка
- 1 — номер помещения, площадь м²

**Допущения и предложения на листе**

Основа листа: размеры сняты с растрового плана заказчика с частичными размерами: рисунок не в масштабе, помещения выровнены по подписанным размерам мебели и проходов; контрольный обмер не выполнен (К-1); высота потолка 2700 мм принята: на плане заказчика её нет (К-2); толщины стен 300 / 120 мм приняты по плану заказчика, не замерены (К-1); разрешённая мощность 15 кВт принята по типовым ТУ для квартиры, ТУ заказчиком не переданы (К-4).

Знак «**» — предложение проектировщика, заказчиком не утверждено (согласовать с заказчиком): записи в реестре нет: AP2, AP1 — точка доступа Wi-Fi: число и места.

Открытые вопросы и конфликты по листу: К-2.

См. лист открытых вопросов (лист 6, записи К-1, К-2, К-4).

## Примечания

1. За отметку ±0,000 принят уровень чистого пола сухих помещений (готовое покрытие), а не существующего пола; пол пом. 7, 9 — −0,015; верх плиты перекрытия −0,064 — расчётный по пирогу пола, не замерен; существующий пол снимается до плиты, его отметка не замерена. Отметки в прямоугольниках — низ потолка; низ плиты перекрытия +2,700. Марка потолка — одна конструкция и отметка на весь альбом.
2. Светильники и потолочные устройства — подложка с планов освещения, слаботочных систем и вентиляции (положение — по ним); вырезы и закладные — по ведомости на листе, до обшивки; отверстия не совмещать с профилями.
3. Пом. 1, 2, 3, 4, 5, 6, 7, 8, 9 — потолок по плите без подвесной системы; отделка — по ведомости отделки.

1000 мм · печать 1:1

| Изм. | Кол.уч | Лист | № док. | Подп. | Дата |
|---|---|---|---|---|---|
| Разраб. | | Кырлан А.С. | | | 18.10.26 |
| Пров. | | | | | |
| ГИП | | | | | |
| | | | | | |
| Н. контр. | | | | | |
| Утв. | | | | | |

**ГД-2026-008-АИ**

Квартира с кабинетом

Общая площадь 127,29* м² · * размеры со скана, не замерены (реестр — л. 6, К-1)

Дизайн-проект интерьера

| Стадия | Лист | Листов |
|---|---|---|
| РП | 34 | 92 |

**План потолков**

М 1:100

**Кырлан Александр Сергеевич**

выпуск 18.10.2026 № d2d5a25dca · стр. 42 из 129

# Раскладка плитки. Планы полов

Раскладка от чистовых размеров · размеры в мм · отметки от ±0,000

ПРЕДВАРИТЕЛЬНО · не для производства работ · открыто пунктов: 4 (реестр — л. 6)

**Фрагмент 1. Ванная (пом. 7). Пол 600×600, шов 2 мм, М 1:40**

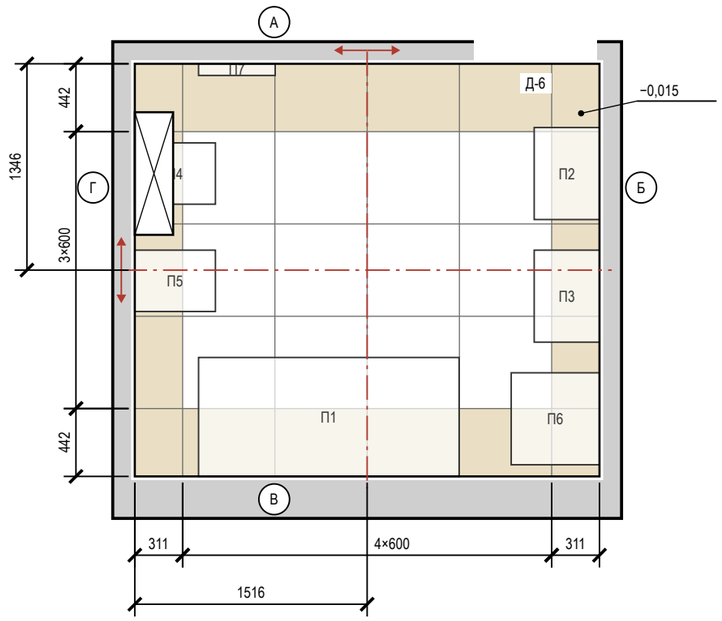


**Фрагмент 2. Санузел гостевой (пом. 9). Пол 600×600, шов 2 мм, М 1:40**

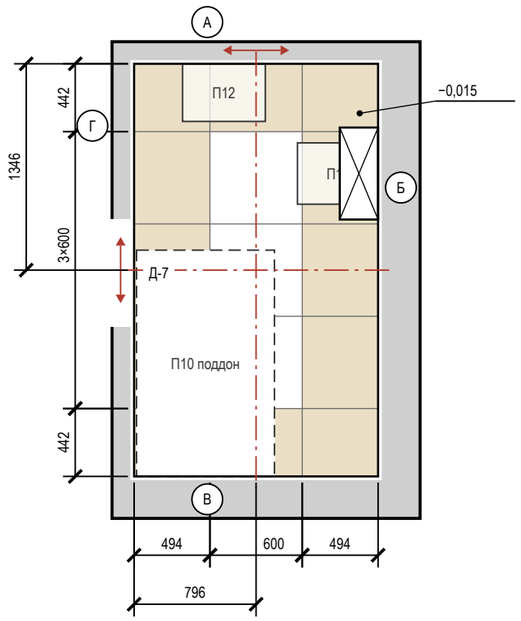


## Ведомость плитки

| Помещение, поверхность | Плитка, код | Формат | Шов | S, м² | Целых | Подр. | С запасом |
|---|---|---|---|---|---|---|---|
| Ванная, пол | аналог: керамогранит под травертин | 600×600 | 2 | 8,44 | 12 | 18 | 33 |
| Ванная, стены А–Г | аналог: керамогранит под травертин | 600×1200 | 2 | 25,34 | 24 | 19 | 49 |
| Ванная, короб инсталляции | аналог: керамогранит под травертин | 600×1200 | 2 | 1,76 | 0 | 6 | 7 |
| Санузел гостевой, пол | аналог: керамогранит под травертин | 600×600 | 2 | 4,49 | 1 | 14 | 17 |
| Санузел гостевой, стены А–Г | аналог: керамогранит под травертин | 600×1200 | 2 | 18,87 | 9 | 22 | 35 |
| Санузел гостевой, короб инсталляции | аналог: керамогранит под травертин | 600×1200 | 2 | 1,47 | 1 | 3 | 5 |
| Прихожая, пол | A8UZ | 600×1200 | 2 | 7,89 | 3 | 12 | 17 |
| Кухня-гостиная, фартук (ст. А) | аналог: керамогранит под травертин, матовый | 1200×600 | 2 | 0,70 | 0 | 2 | 3 |
| Итого 600×600 | | | | 12,93 | 13 | 32 | 50 |
| **Итого 600×1200** | | | | **56,03** | **37** | **64** | **116** |

## Ведомость материалов

| Материал | Класс, код | Норма расхода | Кол-во |
|---|---|---|---|
| Затирка | CG2WA Mapei Ultracolor Plus 132 | (a+b)/ab·шов·t·1,6 | 4,8 кг |
| Затирка | CG2WA | (a+b)/ab·шов·t·1,6 | 0,7 кг |
| Клей | C2 TE S1 Ceresit CM 17 | 1,5 кг/м²·мм, слой 5 | 473 кг (19 меш.) |
| Клей | C2 TE S1 | 1,5 кг/м²·мм, слой 5 | 70 кг (3 меш.) |
| Гидроизоляция | обмазочная, 2 слоя: пол, стены по периметру и зоны замачивания | по ТУ | 28,2 м² |
| Демпф. лента | по периметру пола из плитки | | 28,0 м |

## Условные обозначения

- плитка целая; тонкая линия — шов
- плитка с подрезкой (размер — на цепочке)
- ось старта; стрелки — направление укладки
- сантехприбор: габарит, высота по практике
- поддон душа — плитку пола под ним не кладут
- короб инсталляции: плитка пола — до короба
- отметка чистого пола на полке выноски, м
- А — обозначение стены А–Г (как на развёртках)

## Примечания

1. Раскладка от чистовых размеров: стены санузлов теряют 10 + 5 + 9 = 24 мм на сторону (штукатурка, клей, плитка); подрезки — чистые, без шва.
2. Старт — от центра помещения (штрихпунктир, стрелки — направление укладки); размер старта — от чистовых стен Г и А.
3. Раскладка пола «Прихожая» и фартука «Кухня-гостиная» — на листе «Раскладка плитки. Прихожая. Фартук кухни».
4. Калибр партии не задан — до укладки замерить (рабочий размер W, ГОСТ 13996-2019) и пересчитать подрезки.
5. Количество: целые по раскладке + по одной на подрезку, запас 10 %; один артикул — одна партия и тон. Исключены поддон, короб, проёмы и места за коробом; S — по чистым граням: стены нетто = зона облицовки по ведомости отделки − место за коробом инсталляции 1,68 м² (плитку за коробом не кладут), короб — отдельной строкой.
6. Клей C2 TE S1 Ceresit CM 17; C2 TE S1 (ГОСТ Р 56387-2018), затирка CG2WA Mapei Ultracolor Plus 132; CG2WA; расход — по ТУ выбранной марки.
7. Гидроизоляция: пол и стены 200 мм от ЧП; над ванной — до 2000 и 300 мм за борт, у душа — до 2000 и 500 мм за поддон (см. развёртки); акт скрытых работ, пролив 24 ч.
8. Швы пола совмещены со швами стены А; по периметру — демпферная лента.
9. Отметка чистого пола −0,015, порог 15 мм; стык с соседним покрытием — по оси полотна двери.

**Допущения и предложения на листе**

Основа листа: размеры сняты с растрового плана заказчика с частичными размерами: рисунок не в масштабе, помещения выровнены по подписанным размерам мебели и проходов; контрольный обмер не выполнен (К-1); высота потолка 2700 мм принята: на плане заказчика её нет (К-2); толщины стен 300 / 120 мм приняты по плану заказчика, не замерены (К-1); разрешённая мощность 15 кВт принята по типовым ТУ для квартиры, ТУ заказчиком не переданы (К-4).
См. лист открытых вопросов (лист 6, записи К-1, К-2, К-4).

1000 мм · печать 1:1

| Изм. | Кол.уч | Лист | № док. | Подп. | Дата |
|---|---|---|---|---|---|
| Разраб. | | Кырлан А.С. | | | 18.10.26 |
| Пров. | | | | | |
| ГИП | | | | | |
| | | | | | |
| Н. контр. | | | | | |
| Утв. | | | | | |

**ГД-2026-008-АИ**

Квартира с кабинетом

Общая площадь 127,29* м² · * размеры со скана, не замерены (реестр — л. 6, К-1)

Дизайн-проект интерьера

| Стадия | Лист | Листов |
|---|---|---|
| РП | 35 | 92 |

**Раскладка плитки. Планы полов**

М 1:40

**Кырлан Александр Сергеевич**

выпуск 18.10.2026 № d2d5a25dca · стр. 43 из 129

# Раскладка плитки. Прихожая. Фартук кухни

Раскладка от чистовых размеров · размеры в мм · высоты фартука от чистого пола

**ПРЕДВАРИТЕЛЬНО · не для производства работ · открыто пунктов: 4 (реестр — л. 6)**

**Фрагмент 1. Прихожая (пом. 8). Пол 600×1200, шов 2 мм, М 1:20**

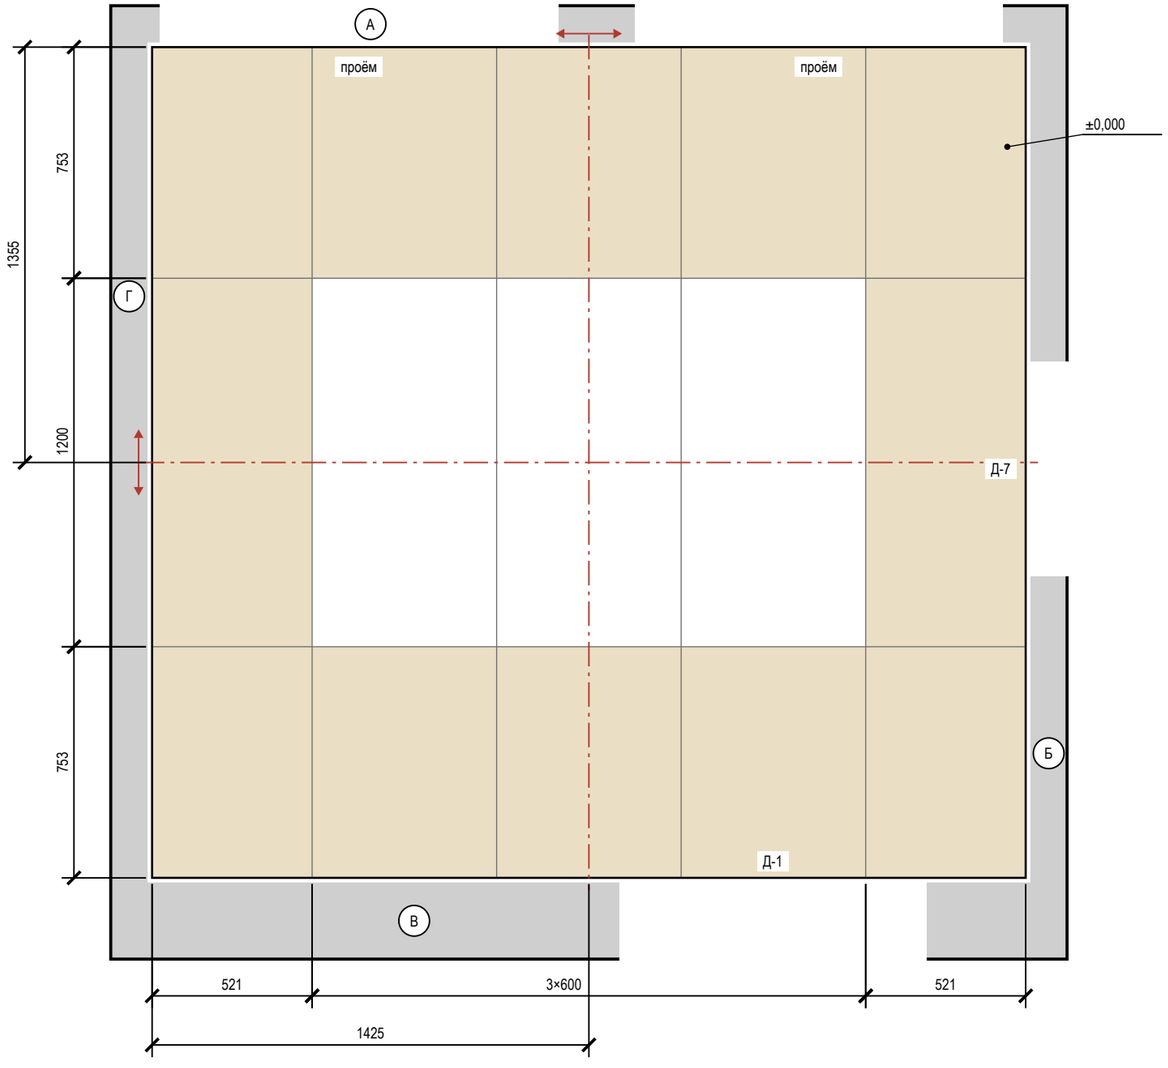


**Фрагмент 2. Кухня-гостиная (пом. 4), фартук, стена А. 1200×600, шов 2 мм, М 1:20**

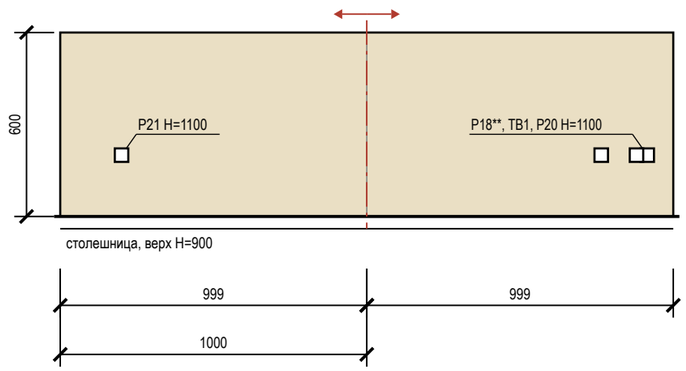


## Условные обозначения

- плитка целая; тонкая линия — шов
- плитка с подрезкой (размер — на цепочке)
- ось старта; стрелки — направление укладки
- электроточка: марка и H — по листам ЭОМ
- столешница (верх)
- навесной шкаф над фартуком
- отметка чистого пола на полке выноски, м
- А — обозначение стены А–Г (как на развёртках)

## Подсчёт плитки

| Поверхность | Формат | S, м² | Целых | Подр. | С запасом |
|---|---|---|---|---|---|
| Прихожая, пол | 600×1200 | 7,89 | 3 | 12 | 17 |
| Кухня-гостиная, фартук (ст. А) | 1200×600 | 0,70 | 0 | 2 | 3 |

## Сдвиг розеток фартука под раскладку

| Точка (ЭОМ) | Проект: от угла / H | Под раскладку: от угла / H | Сдвиг, мм |
|---|---|---|---|
| P18**, TB1, P20 | 1765, 1915, 1880 / 1100 | 1765, 1915, 1880 / 1200 | H +100 — ось ряда |
| P21 | 200 / 1100 | 200 / 1200 | H +100 — ось ряда |

## Примечания

1. Прихожая: керамогранит 600×1200, длинная сторона — вдоль стен Б и Г, шов 2 мм, прямая раскладка от центра. Стены окрашены: раскладка от чистового контура минус штукатурка и шпаклёвка 15 мм на сторону (принято); подрезки 521 / 753 мм, срез — под плинтус.
2. Прихожая: деформационный зазор по периметру 8–10 мм под плинтусом; в проёмах — стык с соседним покрытием по оси полотна двери. Клей C2 TE S1, затирка CG2WA.
3. Фартук, Кухня-гостиная: 1200×600 горизонтально, шов 2 мм; зоны 2000 мм — 900…1500 (от столешницы до низа навесного шкафа, без шкафа — 600 мм). Старт от центра участка, подрезки 999 мм. Площадь 0,70 м² — как в ведомости отделки.
4. Фартук — после монтажа столешницы, низ на 2–3 мм выше неё, шов со столешницей — санитарный герметик; навесные шкафы — после фартука. Торцы у пенала и стены — профиль или запил 45°.
5. Розетки из таблицы переносятся до черновой электрики: по высоте — на ось ряда плитки, от вертикального шва крупной плитки — не ближе 60 мм. Привязка — от левого края фартука на развёртке.
6. Клей, затирка и итог по форматам — в ведомостях листа «Раскладка плитки. Планы полов».

**Допущения и предложения на листе**

Основа листа: размеры сняты с растрового плана заказчика с частичными размерами: рисунок не в масштабе, помещения выровнены по подписанным размерам мебели и проходов; контрольный обмер не выполнен (К-1); высота потолка 2700 мм принята: на плане заказчика её нет (К-2); толщины стен 300 / 120 мм приняты по плану заказчика, не замерены (К-1); разрешённая мощность 15 кВт принята по типовым ТУ для квартиры, ТУ заказчиком не переданы (К-4).

Знак «**» — предложение проектировщика, заказчиком не утверждено (согласовать с заказчиком): записи в реестре нет: P18 — высота 1100 мм выше нормы 1 м (ПУЭ 6.6.30) по назначению: питание ТВ, в одной зоне с выводами TB1 и LAN3; плинтус пом. 4, 8, фартук пом. 4 — артикул изделия не выбран: позиция описана характеристиками («аналог по характеристикам»), артикул выбирается при закупке.

См. лист открытых вопросов (лист 6, записи К-1, К-2, К-4).

1000 мм · печать 1:1

| Изм. | Кол.уч | Лист | № док. | Подп. | Дата | | | | |
|---|---|---|---|---|---|---|---|---|---|
| Разраб. | | Кырлан А.С. | | | 18.10.26 | **ГД-2026-008-АИ** | | | |
| Пров. | | | | | | Квартира с кабинетом<br>Общая площадь 127,29* м² · * размеры со скана, не замерены (реестр — л. 6, К-1) | | | |
| ГИП | | | | | | Дизайн-проект интерьера | Стадия | Лист | Листов |
| | | | | | | | РП | 36 | 92 |
| Н. контр. | | | | | | **Раскладка плитки. Прихожая. Фартук кухни**<br>М 1:20 | **Кырлан Александр Сергеевич** | | |
| Утв. | | | | | | | | | |

# Раскладка плитки. Ванная. Развёртки стен

**ПРЕДВАРИТЕЛЬНО · не для производства работ · открыто пунктов: 4 (реестр — л. 6)**

Пом. 7 · вид изнутри помещения · размеры в мм · высоты от чистого пола, отметки от ±0,000

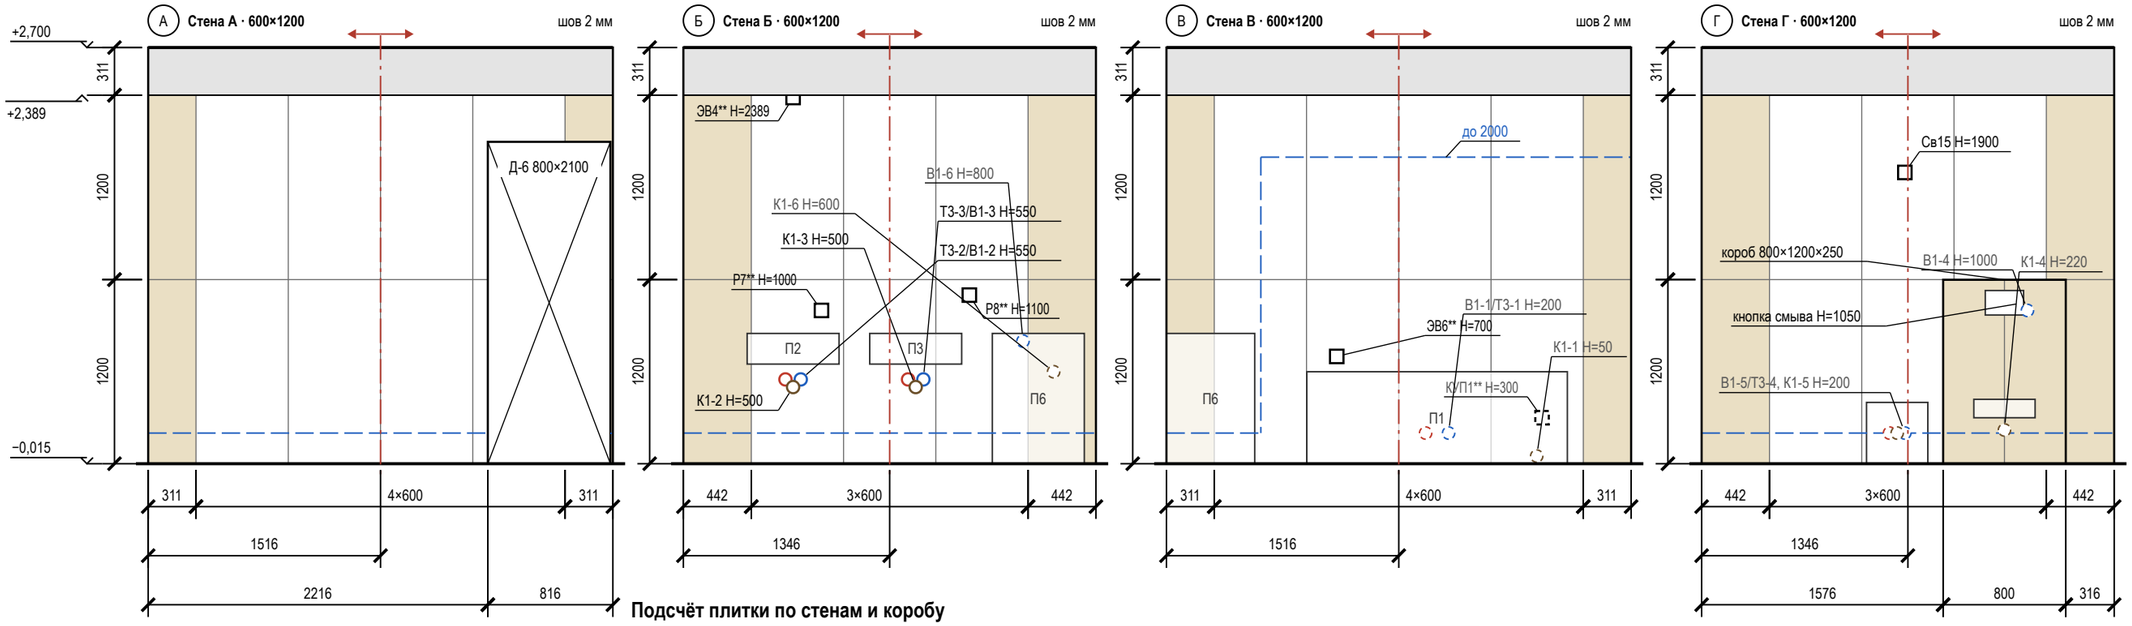


## Условные обозначения

- плитка целая; тонкая линия — шов
- плитка с подрезкой (размер — на цепочке)
- ось старта; стрелки — направление укладки
- верх гидроизоляции: 200 от ЧП, в мокрой зоне — «до …»
- проём — не облицовывается
- сантехприбор: габарит, высота по практике
- короб инсталляции, в нём кнопка смыва 250×160
- вывод В1 (код — в ведомости привязок)
- вывод Т3 (код — в ведомости привязок)
- вывод К1 (код — в ведомости привязок)
- вывод за прибором / в коробе (не на сетке)
- электроточка: марка и Н — по листам ЭОМ
- отметка уровня, м: ±0,000 — чистый пол жилых помещений
- низ потолка; серая полоса — стена без плитки
- А — обозначение стены А–Г (как на развёртках)

## Подсчёт плитки по стенам и коробу

| Поверхность | L × H, мм | S, м² | Целых | Подр. | С запасом | Подрезки: край / верх, мм |
|---|---|---|---|---|---|---|
| стена А | 3032 × 2404 | 5,72 | 6 | 6 | 14 | 311 / 311; целый ряд |
| стена Б | 2692 × 2404 | 6,59 | 6 | 4 | 11 | 442 / 442; целый ряд |
| стена В | 3032 × 2404 | 7,40 | 8 | 4 | 14 | 311 / 311; целый ряд |
| стена Г | 2692 × 2404 | 5,63 | 4 | 5 | 10 | 442 / 442; целый ряд |
| короб (ст. Г) | 800×1200×250 | 1,76 | 0 | 6 | 7 | лицо 399 / 399; бок. 250 |
| **Итого** | | **27,10** | **24** | **25** | **56** | |

## Сдвиг точек под раскладку

| Точка (ВК, ЭОМ) | Стена | Проект: от угла / Н | Под раскладку: от угла / Н | Сдвиг, мм |
|---|---|---|---|---|
| Т3-2/В1-2, К1-2 | Б | 716 / 550, 500 | 744 / 550, 500 | +28 в центр плитки |
| Т3-3/В1-3, К1-3 | Б | 1516 / 550, 500 | 1647 / 550, 500 | +131 на шов |
| P7** | Б | 901 / 1000 | 1045 / 1000 | +144 на шов |
| P8** | Б | 1866 / 1100 | 1948 / 1100 | +82 в центр плитки |
| ЭВ4** | Б | 716 / 2389 | 744 / 2403 | +28 в центр плитки; Н +14 |
| ЭВ6** | В | 1111 / 700 | 1215 / 700 | +104 в центр плитки |
| Св15 | Г | 1326 / 1900 | 1346 / 1900 | +20 в центр плитки |

## Примечания

1. Вид изнутри, стены по часовой стрелке А → Г. Высоты — от чистого пола (−0,015), отметки от ±0,000. Раскладка от чистовых размеров (штукатурка 10 + клей 5 + плитка 9 мм), подрезки чистые; старт — от оси стены, ряды от пола целыми.
2. Верх плитки +2,389, потолок +2,700, зазор 311 мм: потолок ГКЛ опустить до +2,392 (шов 3 мм, герметик) — согласовать с монтажником ГКЛ; иначе профиль-окантовка, полосу окрасить в цвет потолка. Подрезной ряд 306 мм не делать.
3. Точки из таблицы сдвигов переносятся до черновой разводки: смеситель — по оси пары В1 + Т3; вывод на оси прибора — вместе с прибором, иначе старт раскладки — на ось прибора.
4. Выводы — по «Плану выводов сантехники», электроточки — по ЭОМ, «*» — высота по практике; за приборами и в коробе (В1-6, К1-6, В1-1/Т3-1, К1-1, КУП1**, В1-4, К1-4, В1-5/Т3-4, К1-5) штриховым кольцом.
5. Гидроизоляция: 200 мм от ЧП по периметру; над ванной — до 2000 и 300 мм за борт (СП 29.13330.2011, п. 7.2 — на высоту замачивания); углы — лентой; акт скрытых работ, пролив.
6. Короб 800×1200×250: лицо 399 / 399 мм от оси кнопки смыва, боковины, полка; углы — запил 45° или профиль; за коробом плитку не кладут.

**Допущения и предложения на листе**

Основа листа: размеры сняты с растрового плана заказчика с частичными размерами: рисунок не в масштабе, помещения выровнены по подписанным размерам мебели и проходов; контрольный обмер не выполнен (К-1); высота потолка 2700 мм принята: на плане заказчика её нет (К-2); толщины стен 300 / 120 мм приняты по плану заказчика, не замерены (К-1); разрешённая мощность 15 кВт принята по типовым ТУ для квартиры, ТУ заказчиком не переданы (К-4).

Знак «**» — предложение проектировщика, заказчиком не утверждено (согласовать с заказчиком): записи в реестре нет: Р7, Р8 — по образцу: Р7, Р8 и Р33 на высоте 1000 мм — верхний предел нормы (ПУЭ, п. 6.6.30, не выше 1 м); флаг решения снят; ЭВ4, КУП1 — по образцу: Добавлены выводы к вентиляторам: ЭВ4 (ВР1, ванная) и ЭВ5 (ВР3, санузел 2) — группа 3, высота 2389 мм, включение с основным светом, таймер выбега в вентиляторе; и коробки уравнивания потенциалов КУП1 (ванная) и КУП2 (санузел 2) — высота 300 мм, у входа, вне зон 0–2, проводник от шины РЕ щита ЩК, сече; ЭВ6 — по образцу: Добавлены электрические полотенцесушители IP44: П10 в ванной (480 мм, низ 900 мм) и П13 в санузле 2 (400 мм, низ 900 мм), выводы ЭВ6 и ЭВ7; мощность группы 13 — 2,4 кВт вместо 1,8 кВт.

См. лист открытых вопросов (лист 6, записи К-1, К-2, К-4).

1000 мм · печать 1:1

| Изм. | Кол.уч | Лист | № док. | Подп. | Дата |
|---|---|---|---|---|---|
| Разраб. | | Кырлан А.С. | | | 18.10.26 |
| Пров. | | | | | |
| ГИП | | | | | |
| Н. контр. | | | | | |
| Утв. | | | | | |

**ГД-2026-008-АИ**

Квартира с кабинетом

Общая площадь 127,29* м² · * размеры со скана, не замерены (реестр — л. 6, К-1)

Дизайн-проект интерьера

| Стадия | Лист | Листов |
|---|---|---|
| РП | 37 | 92 |

**Раскладка плитки. Ванная. Развёртки стен**

М 1:40

**Кырлан Александр Сергеевич**

выпуск 18.10.2026 № d2d5a25dca · стр. 45 из 129

# Раскладка плитки. Санузел гостевой. Развёртки стен

**ПРЕДВАРИТЕЛЬНО · не для производства работ · открыто пунктов: 4 (реестр — л. 6)**

Пом. 9 · вид изнутри помещения · размеры в мм · высоты от чистого пола, отметки от ±0,000

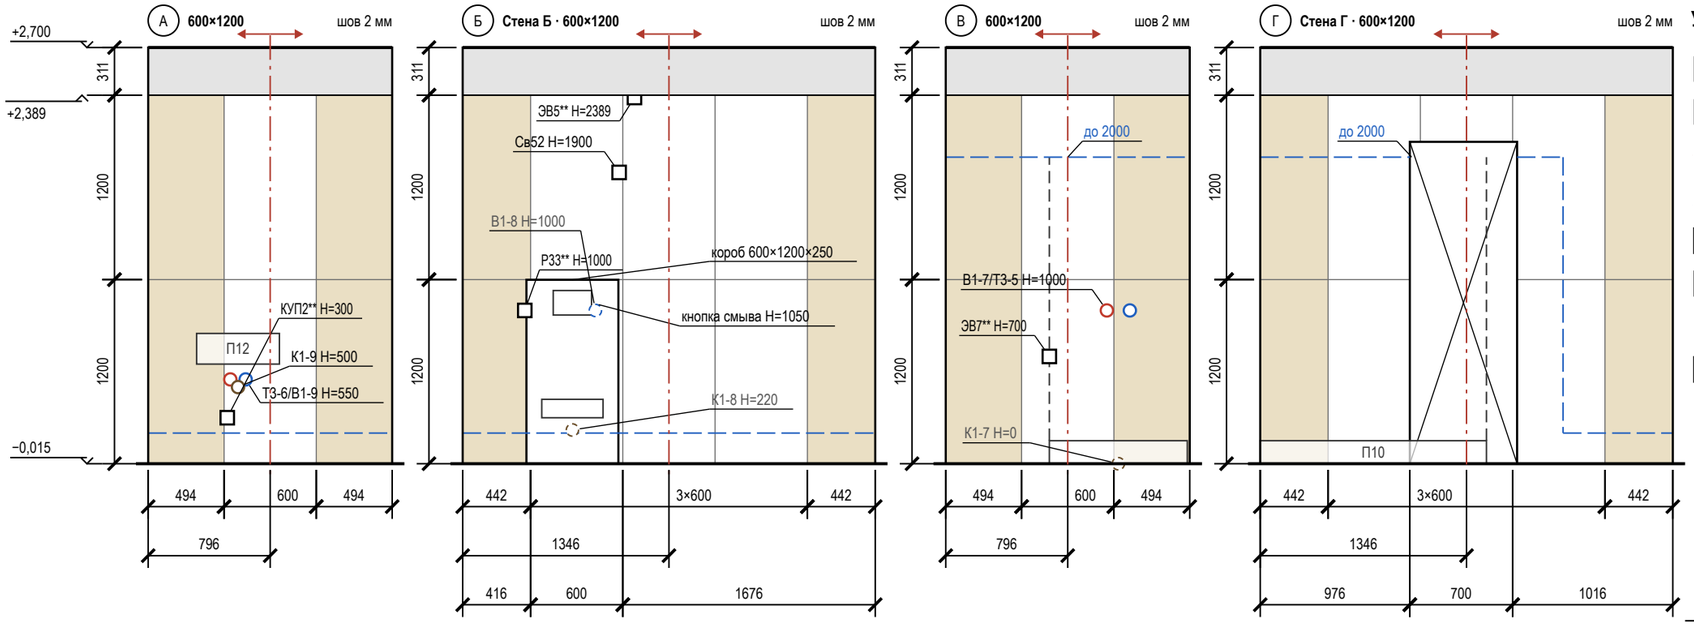


## Условные обозначения

- плитка целая; тонкая линия — шов
- плитка с подрезкой (размер — на цепочке)
- ось старта; стрелки — направление укладки
- верх гидроизоляции: 200 от ЧП, в мокрой зоне — «до …»
- проём — не облицовывается
- сантехприбор: габарит, высота по практике
- граница душевой зоны (ограждение)
- короб инсталляции, в нём кнопка смыва 250×160
- вывод В1 (код — в ведомости привязок)
- вывод Т3 (код — в ведомости привязок)
- вывод К1 (код — в ведомости привязок)
- вывод за прибором / в коробе (не на сетке)
- электроточка: марка и Н — по листам ЭОМ
- отметка уровня, м: ±0,000 — чистый пол жилых помещений
- низ потолка; серая полоса — стена без плитки
- (А) обозначение стены А–Г (как на развёртках)

## Подсчёт плитки по стенам и коробу

| Поверхность | L × H, мм | S, м² | Целых | Подр. | С запасом | Подрезки: край / верх, мм |
|---|---|---|---|---|---|---|
| стена А | 1592 × 2404 | 3,94 | 2 | 4 | 7 | 494 / 494; целый ряд |
| стена Б | 2692 × 2404 | 5,87 | 5 | 5 | 11 | 442 / 442; целый ряд |
| короб (ст. Б) | 600×1200×250 | 1,47 | 1 | 3 | 5 | лицо 600; бок. 250 |
| стена В | 1592 × 2404 | 3,94 | 2 | 4 | 7 | 494 / 494; целый ряд |
| стена Г | 2692 × 2404 | 5,12 | 0 | 9 | 10 | 442 / 442; целый ряд |
| **Итого** | | **20,34** | **10** | **25** | **40** | |

## Сдвиг точек под раскладку

| Точка (ВК, ЭОМ) | Стена | Проект: от угла / Н | Под раскладку: от угла / Н | Сдвиг, мм |
|---|---|---|---|---|
| Т3-6/В1-9, К1-9 | А | 586 / 550, 500 | 495 / 550, 500 | −91 на шов |
| КУП2** | А | 516 / 300 | 495 / 300 | −21 на шов |
| Р33** | Б | 405 / 1000 | 443 / 1000 | +38 на шов |
| Св52 | Б | 1021 / 1900 | 1045 / 1900 | +24 на шов |
| ЭВ5** | Б | 1121 / 2389 | 1045 / 2343 | −76 на шов; Н −46 |
| В1-7/Т3-5 | В | 1126 / 1000 | 1097 / 1000 | −29 на шов |
| ЭВ7** | В | 676 / 700 | 796 / 700 | +120 в центр плитки |

## Примечания

1. Вид изнутри, стены по часовой стрелке А → Г. Высоты — от чистого пола (−0,015), отметки — от ±0,000. Раскладка от чистовых размеров (штукатурка 10 + клей 5 + плитка 9 мм), подрезки чистые; старт — от оси стены, ряды от пола целыми.
2. Верх плитки +2,389, потолок +2,700, зазор 311 мм: потолок ГКЛ опустить до +2,392 (шов 3 мм, герметик) — согласовать с монтажником ГКЛ; иначе профиль-окантовка, полосу окрасить в цвет потолка. Подрезной ряд 306 мм не делать.
3. Точки из таблицы сдвигов переносятся до черновой разводки: смеситель — по оси пары В1 + Т3; вывод на оси прибора — вместе с прибором, иначе старт раскладки — на ось прибора.
4. Выводы — по «Плану выводов сантехники», электроточки — по ЭОМ, «*» — высота по практике; за приборами и в коробе (В1-8, К1-8, К1-7) — штриховым кольцом.
5. Гидроизоляция: 200 мм от ЧП по периметру; у душа — до 2000 и 500 мм за поддон (СП 29.13330.2011, п. 7.2 — на высоту замачивания); углы — лентой; акт скрытых работ, пролив.
6. Короб 600×1200×250: лицо 600 мм от оси кнопки смыва, боковины, полка; углы — запил 45° или профиль; за коробом плитку не кладут.

1000 мм · печать 1:1

**Допущения и предложения на листе**

Основа листа: размеры сняты с растрового плана заказчика с частичными размерами: рисунок не в масштабе, помещения выровнены по подписанным размерам мебели и проходов; контрольный обмер не выполнен (К-1); высота потолка 2700 мм принята: на плане заказчика её нет (К-2); толщины стен 300 / 120 мм приняты по плану заказчика, не замерены (К-1); разрешённая мощность 15 кВт принята по типовым ТУ для квартиры, ТУ заказчиком не переданы (К-4).

Знак «**» — предложение проектировщика, заказчиком не утверждено (согласовать с заказчиком): записи в реестре нет: Р33 — по образцу: Розетка Р33 на высоте 1100 мм, вне шва плитки; ЭВ5, КУП2 — по образцу: Добавлены выводы к вентиляторам: ЭВ4 (ВР1, ванная) и ЭВ5 (ВР3, санузел 2) — группа 3, высота 2389 мм, включение с основным светом, таймер выбега в вентиляторе; и коробки уравнивания потенциалов КУП1 (ванная) и КУП2 (санузел 2) — высота 300 мм, у входа, вне зон 0–2, проводник от шины РЕ щита ЩК, сече; ЭВ7 — по образцу: Добавлены электрические полотенцесушители IP44: П10 в ванной (480 мм, низ 900 мм) и П13 в санузле 2 (400 мм, низ 900 мм), выводы ЭВ6 и ЭВ7; мощность группы 13 — 2,4 кВт вместо 1,8 кВт.

См. лист открытых вопросов (лист 6, записи К-1, К-2, К-4).

| Изм. | Кол.уч | Лист | № док. | Подп. | Дата |
|---|---|---|---|---|---|
| Разраб. | | Кырлан А.С. | | | 18.10.26 |
| Пров. | | | | | |
| ГИП | | | | | |
| | | | | | |
| Н. контр. | | | | | |
| Утв. | | | | | |

**ГД-2026-008-АИ**

Квартира с кабинетом

Общая площадь 127,29* м² · * размеры со скана, не замерены (реестр — л. 6, К-1)

| Дизайн-проект интерьера | Стадия | Лист | Листов |
|---|---|---|---|
| | РП | 38 | 92 |

**Раскладка плитки. Санузел гостевой. Развёртки стен**

М 1:40

**Кырлан Александр Сергеевич**

выпуск 18.10.2026 № d2d5a25dca · стр. 46 из 129

07

# Полы и отделка

Кырлан Александр Сергеевич

выпуск 18.10.2026 · d2d5a25dca · стр. 47 из 129

# План полов

Покрытия, направление укладки, отметки чистого пола, стыки · размеры в мм · отметки в м

## Стыки покрытий в проёмах

| Марка | Проём | Типы пола | Отметки ЧП | Решение |
|---|---|---|---|---|
| СТ1 | 7–5 (Д-6) | 2 / 1 | −0,015 / ±0,000 | порог h=15 мм |
| СТ2 | 8–5 | 3 / 1 | ±0,000 / ±0,000 | б/п |
| СТ3 | 8–4 | 3 / 1 | ±0,000 / ±0,000 | б/п |
| СТ4 | 8–9 (Д-7) | 3 / 2 | ±0,000 / −0,015 | порог h=15 мм |

## Отметки по высоте

| | |
|---|---|
| **±0,000** | чистый пол пом. 1–6, 8; отсчёт высот |
| **−0,015** | чистый пол пом. 7, 9, ниже на 15 мм |
| **−0,064*** | верх плиты — расчёт, не замер (задание на обмер) |
| **сущ. пол** | снимается до плиты; не замерен (задание на обмер) |

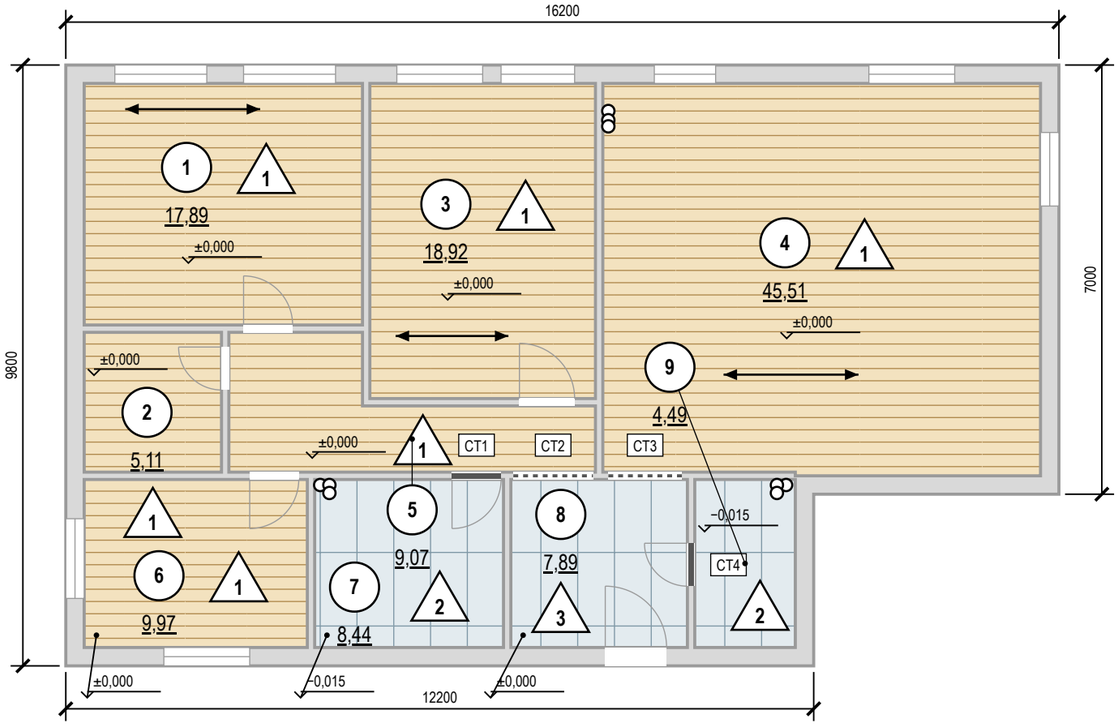


## Экспликация полов

| Номер помещения | Тип пола | Схема пола | Данные элементов пола (наименование, толщина, основание), мм | Площадь, м² |
|---|---|---|---|---|
| 1, 2, 3, 4, 5, 6 | 1 | | Инженерная доска на клею — 14<br>Стяжка ЦПС М200 — 50<br>Плита перекрытия<br>Всего 64 мм; ЧП ±0,000, верх плиты −0,064 | 106,47 |
| 7, 9 | 2 | | Керамогранит на клею С2 TE S1 — 14<br>Гидроизоляция обмазочная, 2 слоя, с заведением на стены 200 мм — 2<br>Стяжка ЦПС М200 — 33<br>Плита перекрытия<br>Всего 49 мм; ЧП −0,015, верх плиты −0,064 | 12,93 |
| 8 | 3 | | Керамогранит на клею С2 TE S1 — 14<br>Стяжка ЦПС М200 — 50<br>Плита перекрытия<br>Всего 64 мм; ЧП ±0,000, верх плиты −0,064 | 7,89 |
| | | | **Итого** | **127,29** |

## Условные обозначения

- тип 1 — инженерная доска, линии — вдоль доски
- тип 2 — керамогранит 600×1200, сетка — формат плитки
- тип 3 — керамогранит 600×1200, сетка — формат плитки
- 1 — номер типа пола (экспликация полов)
- схема пола, без масштаба: плита — штриховка, стяжка — точки, звукоизоляция — зигзаг, гидроизоляция — утолщённая линия с заведением на стену
- направление укладки (длинная сторона доски)
- отметка чистого пола, м
- стык в проёме: порог
- стык в проёме: без порога (б/п)
- СТ1 — марка стыка (ведомость стыков)
- стояк: К1 — канализация, В1 — ХВС, Т3 — ГВС
- 1 — номер помещения, площадь м²

## Примечания

1. За отметку ±0,000 принят чистый пол, не существующий (блок отметок). Площади — по чистым размерам помещений, м²; размеры — в мм.
2. Стык разнотипных покрытий — по оси дверного полотна (под полотном в закрытом положении); решение стыка — по ведомости стыков.
3. Пол санузлов ниже смежных помещений на 15 мм за счёт меньшей толщины стяжки (верх плиты общий — по экспликации полов); гидроизоляция по стяжке с заведением на стены не менее 200 мм (СП 29.13330.2011, п. 7.2), до облицовки — тест проливом и акт скрытых работ.
4. Трубопроводы в конструкции пола не прокладываются: пирог пола 49–64 мм не вмещает выпуски канализации с уклоном — выпуски К1 ведутся по стенам над чистым полом в коробах (лист 31).
5. Звукоизоляционный слой под стяжкой проектом не предусмотрен (стяжка по плите): приведённый уровень ударного шума перекрытия с полом Lnw не более 60 дБ (СП 51.13330.2011, табл. 2) подтвердить по данным дома; при превышении — плавающая стяжка по звукоизоляции с демпферной лентой по контуру и у стояков, пирог пересчитать.
6. Штучные покрытия (инженерная доска): направление — по стрелке; влажность основания по СМ не более 2,0 % (по ТУ изготовителя).
7. Ровность основания — просвет под 2-метровой рейкой не более 2 мм: пом. 1, 2, 3, 4, 5, 6 (инженерная доска), пом. 7, 8, 9 (керамогранит); проверить до укладки покрытия (СП 71.13330.2017, табл. 8.5).
8. Сетка на плитке — условная, в размер формата; точка старта и раскладка — по листу раскладки плитки.
9. Пироги полов — по экспликации полов: слои сверху вниз, толщины в мм; гидроизоляция мокрых зон — в пироге и в ведомости отделки; схема пола — без масштаба.

1000 мм · печать 1:1

**Допущения и предложения на листе**

Основа листа: размеры сняты с растрового плана заказчика с частичными размерами: рисунок не в масштабе, помещения выровнены по подписанным размерам мебели и проходов; контрольный обмер не выполнен (К-1); высота потолка 2700 мм принята: на плане заказчика её нет (К-2); толщины стен 300 / 120 мм приняты по плану заказчика, не замерены (К-1); разрешённая мощность 15 кВт принята по типовым ТУ для квартиры, ТУ заказчиком не переданы (К-4).

Знак «**» — предложение проектировщика, заказчиком не утверждено (согласовать с заказчиком): записи в реестре нет: плинтус пом. 1–5, 8, фартук пом. 4 — артикул изделия не выбран: позиция описана характеристиками («аналог по характеристикам»), артикул выбирается при закупке.

См. лист открытых вопросов (лист 6, записи К-1, К-2, К-4).

| | | | | | | | |
|---|---|---|---|---|---|---|---|
| | | | | | | **ГД-2026-008-АИ** | |
| | | | | | | Квартира с кабинетом | |
| | | | | | | Общая площадь 127,29* м² · * размеры со скана, не замерены (реестр — л. 6, К-1) | |
| Изм. | Кол.уч | Лист | № док. | Подп. | Дата | Дизайн-проект интерьера | Стадия: РП; Лист: 39; Листов: 92 |
| Разраб. | | Кырлан А.С. | | | 18.10.26 | | |
| Пров. | | | | | | | |
| ГИП | | | | | | | |
| Н. контр. | | | | | | **План полов** | **Кырлан Александр Сергеевич** |
| Утв. | | | | | | М 1:100 | |

выпуск 18.10.2026 № d2d5a25dca · стр. 48 из 129

# Ведомость отделки помещений. Лист 1 из 2

ПРЕДВАРИТЕЛЬНО · не для производства работ · открыто пунктов: 4 (реестр — л. 6)

Потолки, стены, низ стен, полы · площади в м², длины в м · отметки в м

### Ведомость отделки помещений (форма 1 прил. А ГОСТ 21.501-2018). Лист 1 из 2

| № | Наименование помещения | Потолок | | | Стены и перегородки | | | Низ стен (плинтус) | | | Пол | | Примечание |
|---|---|---|---|---|---|---|---|---|---|---|---|---|---|
| | | Вид отделки | Код цвета | S, м² | Вид отделки | Код цвета | S, м² | Вид отделки | Код цвета | L, м | Вид отделки | S, м² | |
| 1 | Спальня<br>17,89 м² | Окраска, Tikkurila Anti-Reflex 2, глубокоматовая, 2 слоя, подготовка Q3 | Tikkurila V503 | 17,89 | Окраска, Farrow & Ball Modern Emulsion, матовая, 2 слоя, подготовка Q3<br><br>Акцент — стена А: окраска, Farrow & Ball Modern Emulsion, матовая, 2 слоя, подготовка Q3 | Farrow & Ball No. 15<br><br>Farrow & Ball No. 34 | 31,85<br><br>7,46 | Плинтус МДФ h=80 мм, аналог: МДФ под покраску 80×16 | Farrow & Ball No. 15 | 16,2 | Инженерная доска, 1167-4250, 2100×127 мм, на клею; тип 1, отм. ЧП ±0,000 | 17,89 | Н стен 2700 (до потолка); плинтус в цвет: стены |
| 2 | Гардеробная-постирочная<br>5,11 м² | Окраска, Tikkurila Anti-Reflex 2, глубокоматовая, 2 слоя, подготовка Q3 | Tikkurila V503 | 5,11 | Окраска, Tikkurila Harmony, матовая, 2 слоя, подготовка Q3 | Tikkurila V503 | 22,94 | Плинтус МДФ h=80 мм, аналог: МДФ под покраску 80×16 | Tikkurila V503 | 8,3 | Инженерная доска, 1167-4250, 2100×127 мм, на клею; тип 1, отм. ЧП ±0,000 | 5,11 | Н стен 2700 (до потолка); плинтус в цвет: стены |
| 3 | Кабинет<br>18,92 м² | Окраска, Tikkurila Anti-Reflex 2, глубокоматовая, 2 слоя, подготовка Q3 | Tikkurila V503 | 18,92 | Окраска, Farrow & Ball Modern Emulsion, матовая, 2 слоя, подготовка Q3<br><br>Акцент — стена А: окраска, Farrow & Ball Modern Emulsion, матовая, 2 слоя, подготовка Q3 | Farrow & Ball No. 15<br><br>Farrow & Ball No. 34 | 35,80<br><br>5,78 | Плинтус МДФ h=80 мм, аналог: МДФ под покраску 80×16 | Farrow & Ball No. 15 | 16,7 | Инженерная доска, 1167-4250, 2100×127 мм, на клею; тип 1, отм. ЧП ±0,000 | 18,92 | Н стен 2700 (до потолка); плинтус в цвет: стены |
| 4 | Кухня-гостиная<br>45,51 м² | Окраска, Tikkurila Anti-Reflex 2, глубокоматовая, 2 слоя, подготовка Q3 | Tikkurila V503 | 45,51 | Окраска, Farrow & Ball Modern Emulsion, матовая, 2 слоя, подготовка Q3<br><br>Акцент — стена А: окраска, Farrow & Ball Modern Emulsion, матовая, 2 слоя, подготовка Q3<br>Фартук кухни (стена А): облицовка керамогранитом, аналог: керамогранит под травертин, матовый, 1200×600×9 мм, клей C2 TE S1, затирка CG2WA | Farrow & Ball No. 15<br><br>Farrow & Ball No. 34<br><br>по артикулу | 48,70<br><br>15,64<br><br>0,70 | Плинтус МДФ h=80 мм, аналог: МДФ под покраску 80×16 | Farrow & Ball No. 15 | 25,9 | Инженерная доска, 1167-4250, 2100×127 мм, на клею; тип 1, отм. ЧП ±0,000 | 45,51 | Н стен 2700 (до потолка); матовая моющаяся, класс 1 EN 13300 — осознанно вместо полуматовой; плинтус в цвет: стены |
| 5 | Коридор<br>9,07 м² | Окраска, Tikkurila Anti-Reflex 2, глубокоматовая, 2 слоя, подготовка Q3 | Tikkurila V503 | 9,07 | Окраска, Farrow & Ball Modern Emulsion, матовая, 2 слоя, подготовка Q3 | Farrow & Ball No. 15 | 33,47 | Плинтус МДФ h=80 мм, аналог: МДФ под покраску 80×16 | Farrow & Ball No. 15 | 11,2 | Инженерная доска, 1167-4250, 2100×127 мм, на клею; тип 1, отм. ЧП ±0,000 | 9,07 | Н стен 2700 (до потолка); матовая моющаяся, класс 1 EN 13300 — осознанно вместо полуматовой; плинтус в цвет: стены |
| 6 | Детская<br>9,97 м² | Окраска, Tikkurila Anti-Reflex 2, глубокоматовая, 2 слоя, подготовка Q3 | Tikkurila V503 | 9,97 | Окраска, Farrow & Ball Modern Emulsion, матовая, 2 слоя, подготовка Q3<br><br>Акцент — стена А: окраска, Farrow & Ball Modern Emulsion, матовая, 2 слоя, подготовка Q3 | Farrow & Ball No. 15<br><br>Farrow & Ball No. 34 | 20,30<br><br>8,15 | Плинтус МДФ h=69 мм, SX165 | Farrow & Ball No. 15 | 12,0 | Инженерная доска, 1167-4250, 2100×127 мм, на клею; тип 1, отм. ЧП ±0,000 | 9,97 | Н стен 2700 (до потолка); плинтус в цвет: стены |
| 7 | Ванная<br>8,44 м² | Окраска, Tikkurila Luja 7, матовая, 2 слоя, подготовка Q3 | Tikkurila V503 | 8,44 | Облицовка плиткой, A8UZ, 600×1200×9 мм, клей C2 TE S1, затирка CG2WA | Atlas Concorde A8UZ | 26,30 | нет | | | Керамогранит, A8UZ, 600×1200×9 мм; тип 2, отм. ЧП −0,015 | 8,44 | Н стен 2715 (до потолка); гидроизоляция обмазочная, 2 слоя, с заведением на стены 200 мм (по пирогу пола); тест проливом и акт скрытых работ |
| 8 | Прихожая<br>7,89 м² | Окраска, Tikkurila Anti-Reflex 2, глубокоматовая, 2 слоя, подготовка Q3 | Tikkurila V503 | 7,89 | Окраска, Farrow & Ball Modern Emulsion, матовая, 2 слоя, подготовка Q3 | Farrow & Ball No. 15 | 21,53 | Плинтус МДФ h=80 мм, аналог: МДФ под покраску 80×16 | Farrow & Ball No. 15 | 7,0 | Керамогранит, A8UZ, 600×1200×9 мм; тип 3, отм. ЧП ±0,000 | 7,89 | Н стен 2700 (до потолка); матовая моющаяся, класс 1 EN 13300 — осознанно вместо полуматовой; плинтус в цвет: стены |

## Примечания

1. Ведомость продолжена на листе 2 из 2; итоги, сводка площадей и примечания — на последнем листе ведомости.

**Допущения и предложения на листе**

Основа листа: размеры сняты с растрового плана заказчика с частичными размерами: рисунок не в масштабе, помещения выровнены по подписанным размерам мебели и проходов; контрольный обмер не выполнен (К-1); высота потолка 2700 мм принята: на плане заказчика её нет (К-2); толщины стен 300 / 120 мм приняты по плану заказчика, не замерены (К-1); разрешённая мощность 15 кВт принята по типовым ТУ для квартиры, ТУ заказчиком не переданы (К-4).

Знак «**» — предложение проектировщика, заказчиком не утверждено (согласовать с заказчиком): записи в реестре нет: плинтус пом. 1–5, 8, фартук пом. 4 — артикул изделия не выбран: позиция описана характеристиками («аналог по характеристикам»), артикул выбирается при закупке.

См. лист открытых вопросов (лист 6, записи К-1, К-2, К-4).

| Изм. | Кол.уч | Лист | № док. | Подп. | Дата |
|---|---|---|---|---|---|
| Разраб. | | Кырлан А.С. | | | 18.10.26 |
| Пров. | | | | | |
| ГИП | | | | | |
| | | | | | |
| Н. контр. | | | | | |
| Утв. | | | | | |

**ГД-2026-008-АИ**

Квартира с кабинетом

Общая площадь 127,29* м² · * размеры со скана, не замерены (реестр — л. 6, К-1)

Дизайн-проект интерьера

| Стадия | Лист | Листов |
|---|---|---|
| РП | 40 | 92 |

**Ведомость отделки помещений. Лист 1 из 2**

М б/м

**Кырлан Александр Сергеевич**

выпуск 18.10.2026 № d2d5a25dca · стр. 49 из 129

# Ведомость отделки помещений. Лист 2 из 2

Потолки, стены, низ стен, полы · площади в м², длины в м · отметки в м

## Ведомость отделки помещений (форма 1 прил. А ГОСТ 21.501-2018). Лист 2 из 2

| № | Наименование помещения | Потолок | | | Стены и перегородки | | | Низ стен (плинтус) | | | Пол | | Примечание |
|---|---|---|---|---|---|---|---|---|---|---|---|---|---|
| | | Вид отделки | Код цвета | S, м² | Вид отделки | Код цвета | S, м² | Вид отделки | Код цвета | L, м | Вид отделки | S, м² | |
| 9 | Санузел гостевой<br>4,49 м² | Окраска, Tikkurila Luja 7, матовая,<br>2 слоя, подготовка Q3 | Tikkurila V503 | 4,49 | Облицовка плиткой, A8UZ, 600×1200×9 мм,<br>клей C2 TE S1, затирка CG2WA | Atlas Concorde<br>A8UZ | 19,59 | нет | | | Керамогранит, A8UZ, 600×1200×9 мм;<br>тип 2, отм. ЧП −0,015 | 4,49 | Н стен 2715 (до потолка);<br>гидроизоляция обмазочная, 2<br>слоя, с заведением на стены<br>200 мм (по пирогу пола);<br>тест проливом и акт скрытых<br>работ |
| | **Итого** | | | **127,29** | | | **298,21** | | | **97,3** | | **127,29** | |

## Сводка площадей по материалам отделки

| Поверхность | Материал / код цвета | Серия | Площадь, м² |
|---|---|---|---|
| Потолок | Tikkurila V503 | Anti-Reflex 2 | 114,36 |
| Потолок | Tikkurila V503 | Luja 7 | 12,93 |
| Стены | Farrow & Ball No. 15 | Modern Emulsion | 191,66 |
| Стены | Farrow & Ball No. 34 | Modern Emulsion | 37,02 |
| Стены | Tikkurila V503 | Harmony | 22,94 |
| Стены | облицовка плиткой 600×1200×9 мм,<br>Atlas Concorde A8UZ | A8UZ | 45,89 |
| Фартук | облицовка керамогранитом<br>1200×600×9 мм | аналог: керамогранит<br>под травертин, матовый | 0,70 |

**Допущения и предложения на листе**

Основа листа: размеры сняты с растрового плана заказчика с частичными размерами: рисунок не в масштабе, помещения выровнены по подписанным размерам мебели и проходов; контрольный обмер не выполнен (К-1); высота потолка 2700 мм принята: на плане заказчика её нет (К-2); толщины стен 300 / 120 мм приняты по плану заказчика, не замерены (К-1); разрешённая мощность 15 кВт принята по типовым ТУ для квартиры, ТУ заказчиком не переданы (К-4).

Знак «**» — предложение проектировщика, заказчиком не утверждено (согласовать с заказчиком): записи в реестре нет: плинтус пом. 1–5, 8, фартук пом. 4 — артикул изделия не выбран: позиция описана характеристиками («аналог по характеристикам»), артикул выбирается при закупке.

См. лист открытых вопросов (лист 6, записи К-1, К-2, К-4).

## Примечания

1. Площади поверхностей — по чистым граням стен до отделки: стены = периметр × высоту от чистого пола помещения до низа потолка минус проёмы (облицовка плиткой — до верха облицовки); плинтус = периметр минус дверные проёмы; пол и потолок — по площади помещения. Количество плиток по раскладке. Площади помещений — с учётом всех частей помещения; откосы в площадь стен не входят.
2. Акцентные стены и фартук — отдельными строками, их площадь вычтена из основной отделки стен помещения; фартук — над нижними модулями кухни от столешницы до низа навесных шкафов, где шкафов нет — на 600 мм.
3. Плинтус — длина по периметру за вычетом дверных проёмов; примыкания к наличникам и встроенной мебели — по развёрткам.
4. Формат плитки — Ш×В×Т (ширина × высота в положении укладки × толщина), мм; на полу — вдоль стен А/В × вдоль стен Б/Г.
5. Коды цвета — по веерам производителей; колеровка каждой краски одной партией, проверка выкраса при свете D65 и при лампах проекта.
6. Уровни подготовки Q1–Q4 — система Knauf, не норма ГОСТ/СП; допуски поверхностей — по СП 71.13330.2017 (действующая редакция).
7. «аналог:» — изделие задано характеристиками, марку и артикул согласовать с заказчиком до закупки.

| Изм. | Кол.уч | Лист | № док. | Подп. | Дата |
|---|---|---|---|---|---|
| Разраб. | | Кырлан А.С. | | | 18.10.26 |
| Пров. | | | | | |
| ГИП | | | | | |
| | | | | | |
| Н. контр. | | | | | |
| Утв. | | | | | |

**ГД-2026-008-АИ**

Квартира с кабинетом

Общая площадь 127,29* м² · * размеры со скана, не замерены (реестр — л. 6, К-1)

Дизайн-проект интерьера

| Стадия | Лист | Листов |
|---|---|---|
| РП | 41 | 92 |

**Ведомость отделки помещений. Лист 2 из 2**

М б/м

**Кырлан Александр Сергеевич**

выпуск 18.10.2026 № d2d5a25dca · стр. 50 из 129

# Колерная карта

Цвета и материалы по помещениям · палитра проекта · выкрасы на согласование

## Колерная карта по помещениям

| Помещение | Поверхность | Образец | Поз. | Система и код цвета | Производитель, линейка / материал, артикул | Блеск | Класс EN 13300 | LRV | Площадь |
|---|---|---|---|---|---|---|---|---|---|
| **1. Спальня** 17,89 м² | стены | | **К1** | Farrow & Ball No. 15 | Farrow & Ball · Modern Emulsion | матовая | 1 | 53 | 31,9 м² |
| | акцент А | | **К2** | Farrow & Ball No. 34 | Farrow & Ball · Modern Emulsion | матовая | 1 | 22 | 7,5 м² |
| | потолок | | **К3** | Tikkurila V503 | Tikkurila · Anti-Reflex 2 | глубокомат. | 2 | 86 | 17,9 м² |
| | пол | | **КМ1** | по образцу | Coswick · Вековые традиции | | | | 17,9 м² |
| | плинтус | | **К4** | Farrow & Ball No. 15 | МДФ · в цвет Farrow & Ball | | | 53 | 16,2 м |
| **2. Гардеробная-постирочная** 5,11 м² | стены | | **К5** | Tikkurila V503 | Tikkurila · Harmony | матовая | 1 | 86 | 22,9 м² |
| | потолок | | **К3** | Tikkurila V503 | Tikkurila · Anti-Reflex 2 | глубокомат. | 2 | 86 | 5,1 м² |
| | пол | | **КМ1** | по образцу | Coswick · Вековые традиции | | | | 5,1 м² |
| | плинтус | | **К6** | Tikkurila V503 | МДФ · в цвет Tikkurila | | | 86 | 8,3 м |
| **3. Кабинет** 18,92 м² | стены | | **К1** | Farrow & Ball No. 15 | Farrow & Ball · Modern Emulsion | матовая | 1 | 53 | 35,8 м² |
| | акцент А | | **К2** | Farrow & Ball No. 34 | Farrow & Ball · Modern Emulsion | матовая | 1 | 22 | 5,8 м² |
| | потолок | | **К3** | Tikkurila V503 | Tikkurila · Anti-Reflex 2 | глубокомат. | 2 | 86 | 18,9 м² |
| | пол | | **КМ1** | по образцу | Coswick · Вековые традиции | | | | 18,9 м² |
| | плинтус | | **К4** | Farrow & Ball No. 15 | МДФ · в цвет Farrow & Ball | | | 53 | 16,7 м |
| **4. Кухня-гостиная** 45,51 м² | стены | | **К1** | Farrow & Ball No. 15 | Farrow & Ball · Modern Emulsion | матовая | 1 | 53 | 48,7 м² |
| | акцент А | | **К2** | Farrow & Ball No. 34 | Farrow & Ball · Modern Emulsion | матовая | 1 | 22 | 15,6 м² |
| | потолок | | **К3** | Tikkurila V503 | Tikkurila · Anti-Reflex 2 | глубокомат. | 2 | 86 | 45,5 м² |
| | пол | | **КМ1** | по образцу | Coswick · Вековые традиции | | | | 45,5 м² |
| | плинтус | | **К4** | Farrow & Ball No. 15 | МДФ · в цвет Farrow & Ball | | | 53 | 25,9 м |
| | фартук | | **КМ2** | по образцу | керамогранит · аналог по хар. | | | | 0,7 м² |
| **5. Коридор** 9,07 м² | стены | | **К1** | Farrow & Ball No. 15 | Farrow & Ball · Modern Emulsion | матовая | 1 | 53 | 33,5 м² |
| | потолок | | **К3** | Tikkurila V503 | Tikkurila · Anti-Reflex 2 | глубокомат. | 2 | 86 | 9,1 м² |
| | пол | | **КМ1** | по образцу | Coswick · Вековые традиции | | | | 9,1 м² |
| | плинтус | | **К4** | Farrow & Ball No. 15 | МДФ · в цвет Farrow & Ball | | | 53 | 11,2 м |
| **6. Детская** 9,97 м² | стены | | **К1** | Farrow & Ball No. 15 | Farrow & Ball · Modern Emulsion | матовая | 1 | 53 | 20,3 м² |
| | акцент А | | **К2** | Farrow & Ball No. 34 | Farrow & Ball · Modern Emulsion | матовая | 1 | 22 | 8,1 м² |
| | потолок | | **К3** | Tikkurila V503 | Tikkurila · Anti-Reflex 2 | глубокомат. | 2 | 86 | 10,0 м² |
| | пол | | **КМ1** | по образцу | Coswick · Вековые традиции | | | | 10,0 м² |
| | плинтус | | **К7** | Farrow & Ball No. 15 | Orac Decor · Contour (Luxxus) | | | 53 | 12,0 м |
| **7. Ванная** 8,44 м² | стены | | **К8** | Atlas Concorde A8UZ | Atlas Concorde · Marvel Travertine | | | | 26,3 м² |
| | потолок | | **К9** | Tikkurila V503 | Tikkurila · Luja 7 | матовая | 1 | 86 | 8,4 м² |
| | пол | | **К8** | Atlas Concorde A8UZ | Atlas Concorde · Marvel Travertine | | | | 8,4 м² |
| **8. Прихожая** 7,89 м² | стены | | **К1** | Farrow & Ball No. 15 | Farrow & Ball · Modern Emulsion | матовая | 1 | 53 | 21,5 м² |
| | потолок | | **К3** | Tikkurila V503 | Tikkurila · Anti-Reflex 2 | глубокомат. | 2 | 86 | 7,9 м² |
| | пол | | **К8** | Atlas Concorde A8UZ | Atlas Concorde · Marvel Travertine | | | | 7,9 м² |
| | плинтус | | **К4** | Farrow & Ball No. 15 | МДФ · в цвет Farrow & Ball | | | 53 | 7,0 м |
| **9. Санузел гостевой** 4,49 м² | стены | | **К8** | Atlas Concorde A8UZ | Atlas Concorde · Marvel Travertine | | | | 19,6 м² |
| | потолок | | **К9** | Tikkurila V503 | Tikkurila · Luja 7 | матовая | 1 | 86 | 4,5 м² |
| | пол | | **К8** | Atlas Concorde A8UZ | Atlas Concorde · Marvel Travertine | | | | 4,5 м² |

## Схема палитры проекта

Стиль: Модерн (ар-нуво) 60% + Современный (контемпорари) 40% · схема: аналоговая

| основной | основной | основной | второстепенный | второстепенный | акцентный | акцентный | акцентный |
|---|---|---|---|---|---|---|---|
| Farrow & Ball No. 15 | NCS S 2010-Y30R | Tikkurila V503 | Farrow & Ball No. 34 | Farrow & Ball No. 286 | NCS S 5030-B10G | Farrow & Ball No. 66 | NCS S 8010-Y30R |
| Bone — мягкий каменно-серый с зеленцой LRV 53 стены 1,3,4,5,6,8; плинтус 1,3,4,5,6,8 | Тёплый льняной беж LRV 60 текстиль/декор 1,3,4,6 | Winter LRV 86 потолок 1,2,3,4,5,6,7,8,9; стены 2; плинтус 2; текстиль/декор 1,3,4,6 | Calke Green — традиционный шалфей LRV 22 акцент 1,3,4,6; текстиль/декор 1,3,4,6 | Peignoir — серо-розовый LRV 57 текстиль/декор 3,6 | Павлиний сине-зелёный LRV 12 текстиль/декор 3,6 | India Yellow — глубокая горчица LRV 36 текстиль/декор 3,4,6 | Тёмно-коричневый LRV 3 в отделке не применён |

План 60/30/10

Окраска, факт — по площади стен, акцентов, потолков

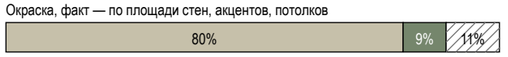


окрашено всего 424,8 м²; второстепенный тон несут мебель и текстиль

**Текстиль и декор в цветах вне палитры проекта**

NCS S 5020-G50Y Оливковый — пом. 1 (Т3)

## Условные обозначения

- **К1** Farrow & Ball No. 15 · Bone — мягкий каменно-серый с зеленцой · Modern Emulsion · матовая · кл. 1
- **К2** Farrow & Ball No. 34 · Calke Green — традиционный шалфей · Modern Emulsion · матовая · кл. 1
- **К3** Tikkurila V503 · Winter · Anti-Reflex 2 · глубокомат. · кл. 2
- **К4** Farrow & Ball No. 15 · Bone — мягкий каменно-серый с зеленцой · МДФ
- **К5** Tikkurila V503 · Winter · Harmony · матовая · кл. 1
- **К6** Tikkurila V503 · Winter · МДФ
- дерево (доска, паркет, ламинат) — рисунок досок
- керамогранит, плитка, камень — сетка швов по формату
- HEX не задан — цвет только по коду и вееру
- **К7** Farrow & Ball No. 15 · Bone — мягкий каменно-серый с зеленцой · Contour (Luxxus)
- **К8** Atlas Concorde A8UZ · Marvel Travertine · Marvel Travertine
- **К9** Tikkurila V503 · Winter · Luja 7 · матовая · кл. 1
- **КМ1** инженерная доска · 1167-4250
- **КМ2** аналог: керамогранит под травертин, матовый, 1200×600×9 мм

К — позиция окраски (код + продукт + блеск), КМ — позиция материала, тон КМ — по описанию артикула, эталон — образец материала; ≈ LRV — расчёт по HEX, справочно

## Перечень выкрасов на согласование

| № | Код | Бренд / веер | Пом. / стена | Подложка | Формат | Статус |
|---|---|---|---|---|---|---|
| 1 | No. 15 | Farrow & Ball | 1, 3, 4, 5, 6, 8 | ГКЛ, загрунтованный под эту краску; МДФ, загрунтованный под эмаль | 600×1000; 300×600 | к выполнению |
| 2 | No. 34 | Farrow & Ball | 1 А, 3 А, 4 А, 6 А | ГКЛ, загрунтованный под эту краску | 600×1000 | к выполнению |
| 3 | V503 | Tikkurila | 1, 2, 3, 4, 5, 6, 7, 8, 9 | ГКЛ, загрунтованный под эту краску; МДФ, загрунтованный под эмаль | 600×1000; 300×600 | к выполнению |

## Примечания

1. Цвет утверждается только по выкрасу на объекте: формат от А3 до 1000×1000 мм на загрунтованном ГКЛ, в 2 слоя (как на стене), не на белой шпаклёвке; смотреть днём и при свете проекта своего помещения, рядом с образцами пола и фасадов. Подпись на обороте: код, бренд и веер, дата.
2. Колеровка машинная в колеровочном центре бренда; каждый код — за один проход, одной партией на весь объём. Колеровщику передаётся только система и код утверждённого веера; плашки и HEX на листе — ориентир, печать не является эталоном цвета.
3. Класс мокрого истирания — EN 13300 (ISO 11998); блеск — по ГОСТ 31975 (ISO 2813), геометрия 60°. LRV — пересчёт координаты L* каталога производителя (Y = ((L*+16)/116)³); «≈» — расчёт по HEX, справочно.
4. Площади поверхностей — тем же способом и с теми же цифрами, что в ведомости отделки (способ счёта — в общих указаниях); объём краски к заказу, фасовка и материалы КМ — в спецификации отделочных материалов.
5. Перечень выкрасов составлен по кодам колерной карты; к основному тону стен добавить на выкрас 2 соседних тона того же веера (светлее и темнее), статус отмечать в графе «Статус» при согласовании.

Допущения и предложения на листе. Знак «**» предложено (согласовать): плинтус пом. 1–5, 8, фартук пом. 4. См. лист открытых вопросов (лист 6).

| Изм. | Кол.уч | Лист | № док. | Подп. | Дата |
|---|---|---|---|---|---|
| Разраб. | | Кырлан А.С. | | | 18.10.26 |
| Пров. | | | | | |
| ГИП | | | | | |
| | | | | | |
| Н. контр. | | | | | |
| Утв. | | | | | |

**ГД-2026-008-АИ**

Квартира с кабинетом

Общая площадь 127,29* м² · * размеры со скана, не замерены (реестр — л. 6, К-1)

Дизайн-проект интерьера

| Стадия | Лист | Листов |
|---|---|---|
| РП | 42 | 92 |

**Колерная карта**

М б/м

**Кырлан Александр Сергеевич**

выпуск 18.10.2026 № d2d5a25dca · стр. 51 из 129

# Спецификация отделочных материалов

**ПРЕДВАРИТЕЛЬНО · не для производства работ · открыто пунктов: 4 (реестр — л. 6)**

Форма 1 по ГОСТ 21.110-2013 · количества — из геометрии проекта, с запасом

| Поз. | Наименование и техническая характеристика | Тип, марка, обозначение документа | Код продукции | Поставщик | Ед. изм. | Кол. | Масса 1 ед., кг | Примечание |
|---|---|---|---|---|---|---|---|---|
| | **Лакокрасочные материалы** | | | | | | | |
| 1 | Краска интерьерная водно-дисперсионная акриловая для стен, матовая, класс мокрого истирания 1 по EN 13300, база A; цвет Farrow & Ball No. 15 «Bone — мягкий каменно-серый с зеленцой», колеровка машинная | Farrow & Ball Modern Emulsion | | Farrow & Ball | л | 52,5 | | поз. К1 колерной карты; пом. 1, 3, 4, 5, 6, 8; S = 191,7 м² × 2 сл. × 0,12 л/м² = 46,0 л, +10 % и 0,5 л на подкраску → ≥ 51,1 л; тара 10 × 5 л + 1 × 2,5 л |
| 2 | Краска интерьерная водно-дисперсионная акриловая для акцентных стен, матовая, класс мокрого истирания 1 по EN 13300, база C; цвет Farrow & Ball No. 34 «Calke Green — традиционный шалфей», колеровка машинная | Farrow & Ball Modern Emulsion | | Farrow & Ball | л | 12,5 | | поз. К2 колерной карты; пом. 1, 3, 4, 6; S = 37,0 м² × 2 сл. × 0,12 л/м² = 8,9 л, +10 % и 0,5 л на подкраску → ≥ 10,3 л; тара 2 × 5 л + 1 × 2,5 л |
| 3 | Краска интерьерная водно-дисперсионная акриловая для потолков, глубокоматовая, класс мокрого истирания 2 по EN 13300, база A; цвет Tikkurila V503 «Winter», колеровка машинная | Tikkurila Anti-Reflex 2 | | Tikkurila | л | 31,5 | | поз. К3 колерной карты; пом. 1, 2, 3, 4, 5, 6, 8; S = 114,4 м² × 2 сл. × 0,12 л/м² = 27,4 л, +10 % и 0,5 л на подкраску → ≥ 30,7 л; тара 3 × 9 л + 1 × 2,7 л + 2 × 0,9 л |
| 4 | Краска интерьерная водно-дисперсионная акриловая для стен, матовая, класс мокрого истирания 1 по EN 13300, база A; цвет Tikkurila V503 «Winter», колеровка машинная | Tikkurila Harmony | | Tikkurila | л | 7,2 | | поз. К5 колерной карты; пом. 2; S = 22,9 м² × 2 сл. × 0,12 л/м² = 5,5 л, +10 % и 0,5 л на подкраску → ≥ 6,6 л; тара 2 × 2,7 л + 2 × 0,9 л |
| 5 | Краска интерьерная водно-дисперсионная акриловая для потолков, матовая, класс мокрого истирания 1 по EN 13300, база A; цвет Tikkurila V503 «Winter», колеровка машинная | Tikkurila Luja 7 | | Tikkurila | л | 4,5 | | поз. К9 колерной карты; пом. 7, 9; S = 12,9 м² × 2 сл. × 0,12 л/м² = 3,1 л, +10 % и 0,5 л на подкраску → ≥ 3,9 л; тара 1 × 2,7 л + 2 × 0,9 л |
| 6 | Краска для МДФ и дерева в цвет Farrow & Ball No. 15 «Bone — мягкий каменно-серый с зеленцой» — окраска плинтуса; блеск не ниже блеска стен | марка не задана | | | л | 2,3 | | поз. К4, К7; пом. 1, 3, 4, 5, 6, 8; L = 89,0 м, S = 8,4 м² × 2 сл. × 0,12 л/м² + 10 %; продукт подобрать в веере Farrow & Ball |
| 7 | Краска для МДФ и дерева в цвет Tikkurila V503 «Winter» — окраска плинтуса; блеск не ниже блеска стен | марка не задана | | | л | 0,5 | | поз. К6; пом. 2; L = 8,3 м, S = 0,8 м² × 2 сл. × 0,12 л/м² + 10 %; продукт подобрать в веере Tikkurila |
| 8 | Грунтовка акриловая под окраску стен и потолков — из системы производителя краски | по системе краски | | | м² | 379 | | площадь окраски стен, акцентов и потолков; 1 слой перед окраской; расход — по ТУ грунтовки |
| | **Плитка и керамогранит** | | | | | | | |
| 9 | Керамогранит под травертин, 600×600 мм | аналог по характеристикам | | | м² | 18 | | шов 2 мм; Ванная, пол; Санузел гостевой, пол; по раскладке 45 шт (S = 12,93 м²), с запасом 50 шт |
| 10 | Керамогранит под травертин, 600×1200×9 мм, ректификат, водопоглощение 0,1 % | аналог по характеристикам | | Atlas Concorde | м² | 69,12 | | шов 2 мм; Ванная, стены А–Г; Ванная, короб инсталляции; Санузел гостевой, стены А–Г; Санузел гостевой, короб инсталляции; по раскладке 84 шт (S = 47,44 м²), с запасом 96 шт |
| 11 | A8UZ, 600×1200×9 мм, ректификат, водопоглощение 0,1 % (BIa), противоскольжение R10, PEI IV | A8UZ | | Atlas Concorde | м² | 12,24 | | шов 2 мм; Прихожая, пол; по раскладке 15 шт (S = 7,89 м²), с запасом 17 шт |
| 12 | Керамогранит под травертин, матовый, 1200×600×9 мм, ректификат, водопоглощение 0,1 % (BIa) | аналог по характеристикам | | | м² | 2,16 | | шов 2 мм; Кухня-гостиная, фартук (ст. А); по раскладке 2 шт (S = 0,70 м²), с запасом 3 шт |
| | **Напольные покрытия** | | | | | | | |
| 13 | 1167-4250, рабочий слой 4 мм, эмиссия E1, укладка на клей | 1167-4250 | | Coswick | м² | 114 | | пом. 1, 2, 3, 4, 5, 6; S = 106,47 м² + 7 % (прямая укладка); к заказу — кратно упаковке |
| 14 | Клей для паркета и инженерной доски, эластичный (СМП / полиуретановый) | по рекомендации производителя доски | | | м² | 107 | | площадь приклейки; расход и шпатель — по ТУ клея |
| | **Погонажные изделия** | | | | | | | |
| 15 | Плинтус МДФ под покраску 80×16, крепление к стене, окраска в цвет Farrow & Ball No. 15 | аналог по характеристикам | | | м | 94 | | пом. 1, 2, 3, 4, 5, 8; L = 85,4 м (периметр без дверных проёмов) + 10 % на подрезку; в штуках — по длине планки |
| 16 | SX165, h = 69 мм, крепление к стене, окраска в цвет Farrow & Ball No. 15 | SX165 | | Orac Decor | м | 14 | | пом. 6; L = 12,0 м (периметр без дверных проёмов) + 10 % на подрезку; в штуках — по длине планки |
| | **Смеси и материалы для облицовки** | | | | | | | |
| 17 | Затирка для швов плитки, класс CG2WA по EN 13888 | Mapei Ultracolor Plus 132 | | Mapei | кг | 5,5 | | по раскладке (a+b)/(a·b) × шов × t × 1,6 + 10 %; в т. ч. 0,7 кг — позиции раскладки без марки |
| 18 | Клей плиточный C2 TE S1 по EN 12004, слой 5 мм | Ceresit CM 17 | | Ceresit | кг | 543 | | 22 меш. по 25 кг; 1,5 кг/м² на 1 мм слоя + 10 %; в т. ч. 70 кг — позиции раскладки без марки |
| 19 | Гидроизоляция обмазочная мокрых зон: пол, стены по периметру, зоны замачивания; 2 слоя с армирующей лентой в углах | аналог по характеристикам | | | м² | 28,2 | | площадь по листу раскладки плитки + 10 %; расход смеси — по ТУ |
| 20 | Лента демпферная по периметру пола из плитки | аналог по характеристикам | | | м | 28 | | периметр без дверных проёмов + 10 % |

## Примечания

1. Количества — из геометрии проекта: площади поверхностей по чистым граням стен до отделки (те же, что в ведомости отделки и колерной карте), плитка, клей и затирка — по раскладке плиточника; в графе «Кол.» — к заказу, с запасом.
2. Краска: расход 0,12 л/м² на слой в 2 слоя, если по ТУ не задан иной; запас 10 % и 0,5 л на подкраску каждого кода. Один код — одна партия, колеровка машинная в колеровочном центре бренда; в заказ — только после утверждения выкраса (колерная карта). Фасовка — по каталогу бренда на дату выпуска; к заказу — не меньше расчётного объёма.
3. «Аналог по характеристикам» — допускается изделие другого производителя с характеристиками не ниже указанных, по согласованию с автором проекта.
4. Графы «Код продукции» и «Масса 1 ед.» не заполнены: коды по классификатору продукции не присвоены, масса единицы до 25 кг (ГОСТ 21.110-2013).
5. Грунтовка и клей для доски указаны площадью обработки; объём — по ТУ выбранного продукта.

**Допущения и предложения на листе**

Основа листа: размеры сняты с растрового плана заказчика с частичными размерами: рисунок не в масштабе, помещения выровнены по подписанным размерам мебели и проходов; контрольный обмер не выполнен (К-1); высота потолка 2700 мм принята: на плане заказчика её нет (К-2); толщины стен 300 / 120 мм приняты по плану заказчика, не замерены (К-1); разрешённая мощность 15 кВт принята по типовым ТУ для квартиры, ТУ заказчиком не переданы (К-4).

Знак «**» — предложение проектировщика, заказчиком не утверждено (согласовать с заказчиком): записи в реестре нет: плинтус пом. 1–5, 8, фартук пом. 4 — артикул изделия не выбран: позиция описана характеристиками («аналог по характеристикам»), артикул выбирается при закупке.

См. лист открытых вопросов (лист 6, записи К-1, К-2, К-4).

| Изм. | Кол.уч | Лист | № док. | Подп. | Дата |
|---|---|---|---|---|---|
| Разраб. | | Кырлан А.С. | | | 18.10.26 |
| Пров. | | | | | |
| ГИП | | | | | |
| | | | | | |
| Н. контр. | | | | | |
| Утв. | | | | | |

**ГД-2026-008-АИ**

Квартира с кабинетом

Общая площадь 127,29* м² · * размеры со скана, не замерены (реестр — л. 6, К-1)

| | Стадия | Лист | Листов |
|---|---|---|---|
| Дизайн-проект интерьера | РП | 43 | 92 |
| **Спецификация отделочных материалов** М б/м | **Кырлан Александр Сергеевич** | | |

# Концепция декора и визуализации

Модерн (ар-нуво) · современный модерн · визуализации, палитра, материалы, ключевые предметы

**Визуализация 1. Вид сверху (3D): планировка с мебелью, текстилем и декором**

Расстановка — по плану мебели (лист 16); шторы, ковры, картины и растения — по плану текстиля и декора (лист 45).

**Визуализация 17. Кухня-гостиная (пом. 4)**

шторы Т13, Т14, Т15 · ковёр Т16 · картина ДК6 · растение ДК7 · подушки, пледы Т17, Т18, Т19

**Визуализация 7. Спальня (пом. 1)**

шторы Т1, Т2 · ковёр Т3 · картина ДК1 · подушки, пледы Т4, Т5, Т6

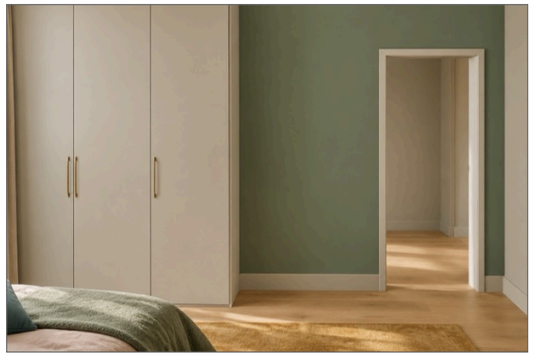

**Визуализация 14. Детская (пом. 6)**

шторы Т20, Т21 · ковёр Т22 · картина ДК2 · зеркало ДК5 · подушки, пледы Т23, Т24, Т25

**Визуализация 21. Кабинет (пом. 3)**

шторы Т7, Т8 · ковёр Т9 · картина ДК3 · зеркало ДК4 · подушки, пледы Т10, Т11, Т12

## Материалы и фактуры

**Дуб натуральный**
пол: пом. 1, 2, 3, 4, 5, 6; рамы ДК1, ДК2, ДК3

**Травертин (керамогранит)**
пол и стены санузлов, фартук: пом. 4

**Букле**
подушки: Т10, Т17, Т23

**Лён**
портьеры, подушки, римская штора: Т1, Т4, Т7, Т13, Т15, Т20

**Бронза и чёрный металл**
рамы ДК4, ДК5, ДК9 — чёрный; фурнитура, светильники — бронза

## Палитра 60/30/10 и цвета текстиля

- Farrow & Ball No. 15 (Bone — мягкий каменно-серый с зеленцой), LRV 53 — 60 % база
- Tikkurila V503 (Winter), LRV 86 — 60 % база — Т2, Т8, Т14, Т21
- Farrow & Ball No. 286 (Peignoir — серо-розовый), LRV 57 — 30 % второй цвет — Т10, Т23
- Farrow & Ball No. 66 (India Yellow — глубокая горчица), LRV 36 — 10 % акцент — Т9, Т15, Т16, Т19, Т22
- NCS S 5020-G50Y (Оливковый), LRV 18 — акцент текстиля — Т3
- NCS S 2010-Y30R (Тёплый льняной беж), LRV 60 — 60 % база — Т1, Т4, Т7, Т13, Т17, Т20
- Farrow & Ball No. 34 (Calke Green — традиционный шалфей), LRV 22 — 30 % второй цвет — Т5, Т6, Т12, Т18, Т25
- NCS S 5030-B10G (Павлиний сине-зелёный), LRV 12 — 10 % акцент — Т11, Т24
- NCS S 8010-Y30R (Тёмно-коричневый), LRV 3 — 10 % акцент

## Ключевые предметы

— Диван К4 2150×950 — кабинет; подушки и плед Т10, Т11, Т12
— Диван Кх9 1000×2700 — кухня-гостиная; подушки и плед Т17, Т18, Т19
— Кровати Д2, С1 — над изголовьем картины ДК1, ДК2; текстиль Т4, Т5, Т6, Т23, Т24, Т25
— Ковры Т3, Т9, Т16, Т22 — шерсть, на противоскользящей подложке
— Картины ДК1, ДК2, ДК3, ДК6 — центр на высоте 1350–1650 мм
— Зеркала в рост ДК4, ДК5, ДК9
— Шторы-волна Т1, Т7, Т13, Т20 (NCS S 2010-Y30R), тюль Т2, Т8, Т14, Т21 (Tikkurila V503) — в нишах потолка
— Растение ДК7, ваза ДК8

## Настроение

Современный модерн 2026: модерн 60 % + современный (contemporary.json) 40 %. Стены — Bone No. 15 и льняной беж S 2010-Y30R, потолки — Winter V503, шалфей Calke Green No. 34 и пудровый Peignoir No. 286 вторым планом, акценты — павлиний S 5030-B10G (бархат), горчица India Yellow No. 66, морёный дуб S 8010-Y30R; металл — латунь. Настроение стиля: природность, плавность, камерность, ремесленность, поэтичность, приглушённая цветность, сумеречный тёплый свет. Свет тёплый, 2200–2700 K.

## Примечания

1. Визуализации — образ интерьера. Изделия, размеры, высоты подвеса и привязки — по чертежам (план текстиля и декора — лист 45; шторы и карнизы — лист 46; ведомость текстиля — лист 47; ведомость декора и развеска — лист 48); при расхождении действуют чертежи и ведомости.
2. Коды цвета — ориентир подбора по веерам производителей; ткань утверждается по образцу при дневном свете и при свете проекта 2700–3000 K.
3. Мелкий стайлинг на визуализациях (книги, посуда, свечи) в ведомости не входит и поставляется заказчиком по желанию.

**Допущения и предложения на листе**

Основа листа: размеры сняты с растрового плана заказчика с частичными размерами: рисунок не в масштабе, помещения выровнены по подписанным размерам мебели и проходов; контрольный обмер не выполнен (К-1); высота потолка 2700 мм принята: на плане заказчика её нет (К-2); толщины стен 300 / 120 мм приняты по плану заказчика, не замерены (К-1); разрешённая мощность 15 кВт принята по типовым ТУ для квартиры, ТУ заказчиком не переданы (К-4).
См. лист открытых вопросов (лист 6, записи К-1, К-2, К-4).

| | | | | | | | | | |
|---|---|---|---|---|---|---|---|---|---|
| | | | | | | **ГД-2026-008-АИ** | | | |
| | | | | | | Квартира с кабинетом<br>Общая площадь 127,29* м² · * размеры со скана, не замерены (реестр — л. 6, К-1) | | | |
| Изм. | Кол.уч | Лист | № док. | Подп. | Дата | Дизайн-проект интерьера | Стадия | Лист | Листов |
| Разраб. | | Кырлан А.С. | | | 18.10.26 | | РП | 44 | 92 |
| Пров. | | | | | | | | | |
| ГИП | | | | | | | | | |
| | | | | | | **Концепция декора и визуализации**<br>М б/м | **Кырлан Александр Сергеевич** | | |
| Н. контр. | | | | | | | | | |
| Утв. | | | | | | | | | |

# План текстиля и декора

Шторы и карнизы, ковры, картины и зеркала, растения · размеры в мм от чистовых стен и чистого пола · марки — по ведомостям

**ПРЕДВАРИТЕЛЬНО · не для производства работ · открыто пунктов: 4 (реестр — л. 6)**

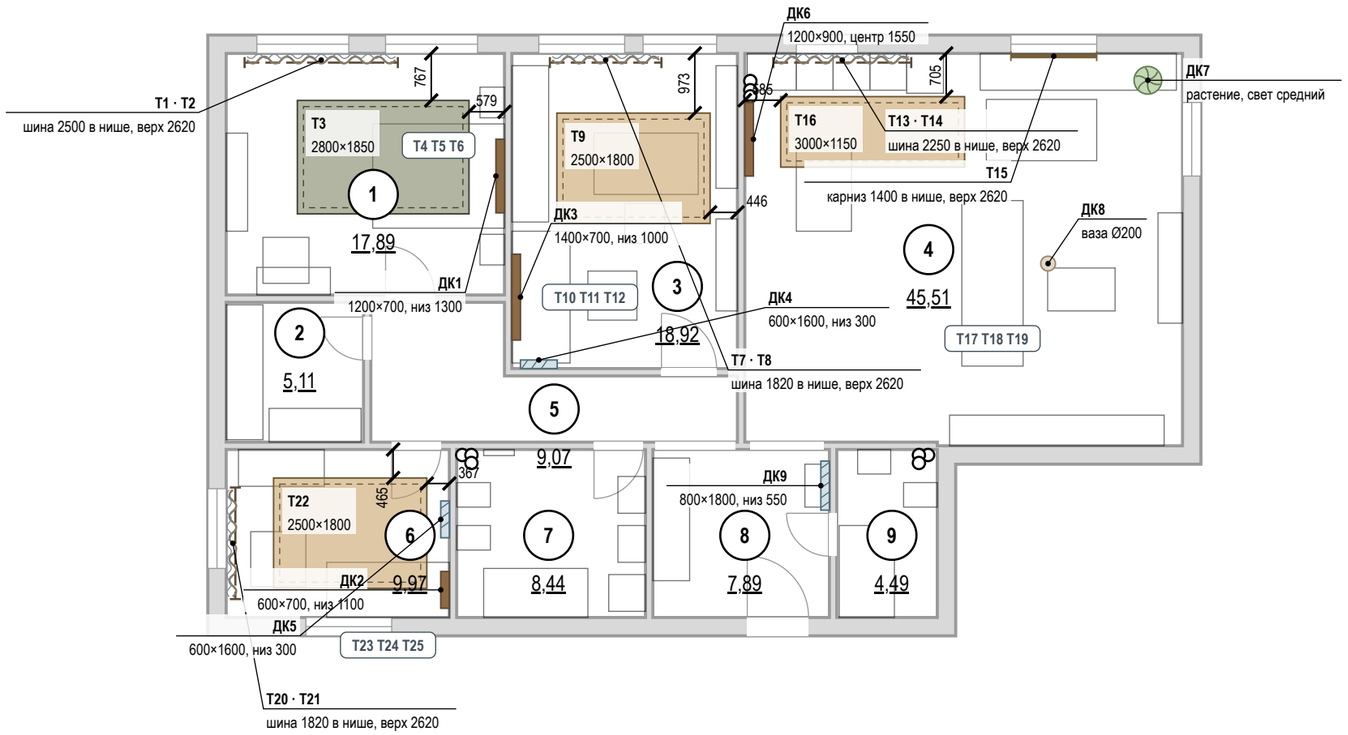


## Условные обозначения

- ковёр — габарит в масштабе, цвет изделия
- шина или карниз штор (выше плоскости разреза)
- портьеры (штора-волна)
- тюль (на плане — волнистая линия)
- римская или рулонная штора в проёме
- картина на стене — ширина в масштабе
- зеркало на стене — ширина в масштабе
- растение в кашпо — диаметр в масштабе
- ваза, настольный декор
- подушки, пледы — марки на мебели
- привязка от чистовой стены, мм
- (1) номер помещения, площадь м²
- стены (подложка обмера)

Т1, ДК1 — марки по ведомостям текстиля и декора

**Экспликация помещений**

лист 12 · на плане — номера в марках

## Окна: шина → полотно, мм

| Поз. | Шина | Верх шины | Полотно, низ |
|---|---|---|---|
| Т1, Т2 | 2500 | 2620, ниша | 2610, низ 10 |
| Т7, Т8 | 1820 | 2620, ниша | 2610, низ 10 |
| Т13, Т14 | 2250 | 2620, ниша | 2610, низ 10 |
| Т15 | 1400 | 2620, ниша | 1620, низ 1000 |
| Т20, Т21 | 1820 | 2620, ниша | 2610, низ 10 |

## Развеска: высоты от пола, мм

| Поз. | Пом. | Ш×В | Центр | Низ | Стена |
|---|---|---|---|---|---|
| ДК1 | 1 | 1200×700 | 1650 | 1300 | Б |
| ДК2 | 6 | 600×700 | 1450 | 1100 | Б |
| ДК3 | 3 | 1400×700 | 1350 | 1000 | Г |
| ДК4 | 3 | 600×1600 | 1100 | 300 | В |
| ДК5 | 6 | 600×1600 | 1100 | 300 | Б |
| ДК6 | 4 | 1200×900 | 1550 | 1100 | Г |
| ДК9 | 8 | 800×1800 | 1450 | 550 | Б |

**Допущения и предложения на листе**

Основа листа: размеры сняты с растрового плана заказчика с частичными размерами: рисунок не в масштабе, помещения выровнены по подписанным размерам мебели и проходов; контрольный обмер не выполнен (К-1); высота потолка 2700 мм принята: на плане заказчика её нет (К-2); толщины стен 300 / 120 мм приняты по плану заказчика, не замерены (К-1); разрешённая мощность 15 кВт принята по типовым ТУ для квартиры, ТУ заказчиком не переданы (К-4).

См. лист открытых вопросов (лист 6, записи К-1, К-2, К-4).

## Примечания

1. Размеры — в мм. Отступы ковров — от чистовых стен; высоты картин и зеркал — от чистого пола до центра или низа рамы.
2. Шторы — на шинах в нишах потолка (ниша — план потолков, лист 34); закладная под шину — до обшивки ГКЛ. Схемы окон, длины полотен и сборка — лист 46.
3. Картины и зеркала массой более 5 кг — на анкеры по основанию, нагрузка крепежа не меньше двойной массы изделия; на ГКЛ — только по закладной. Декор не перекрывает розетки и выключатели.
4. Ковры на гладком полу — на противоскользящей подложке.
5. Мебель — по плану расстановки мебели (лист 16); ведомость текстиля — лист 47, ведомость декора и схемы развески — лист 48.
6. Номера помещений — по экспликации (лист 12); наименования и площади на этом листе не дублируются.
7. Марки текстиля «Т» и декора «Д» относятся только к листам текстиля и декора; индексы трубопроводов Т1–Т4 — на листах ВК и ОВ.

1000 мм · печать 1:1

| Изм. | Кол.уч | Лист | № док. | Подп. | Дата |
|---|---|---|---|---|---|
| Разраб. | | Кырлан А.С. | | | 18.10.26 |
| Пров. | | | | | |
| ГИП | | | | | |
| Н. контр. | | | | | |
| Утв. | | | | | |

**ГД-2026-008-АИ**

Квартира с кабинетом

Общая площадь 127,29* м² · * размеры со скана, не замерены (реестр — л. 6, К-1)

Дизайн-проект интерьера

| Стадия | Лист | Листов |
|---|---|---|
| РП | 45 | 92 |

**План текстиля и декора**

М 1:100

**Кырлан Александр Сергеевич**

08

# Декор и текстиль

Кырлан Александр Сергеевич

выпуск 18.10.2026 · d2d5a25dca · стр. 55 из 129

# Шторы и карнизы

Схемы окон «шина → полотно» (М 1:100) · отметки от чистого пола помещения · размеры в мм

**Окно 1 — Спальня (пом. 1): Т1, Т2 (М 1:100)**

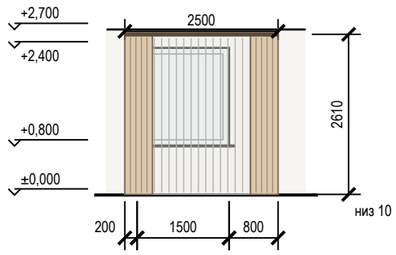


**Окно 1 — Кабинет (пом. 3): Т7, Т8 (М 1:100)**

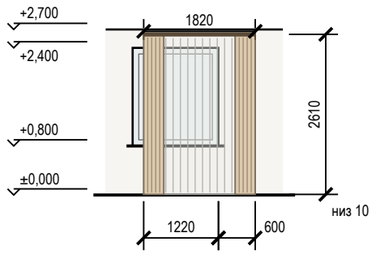


**Окно 1 — Кухня-гостиная (пом. 4): Т13, Т14 (М 1:100)**

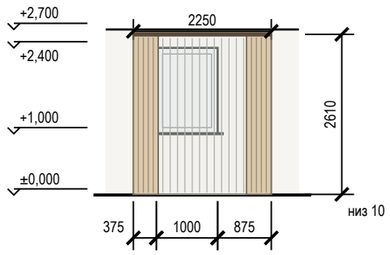


**Окно 2 — Кухня-гостиная (пом. 4): Т15 (М 1:100)**

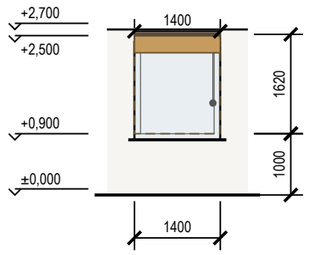


**Окно 1 — Детская (пом. 6): Т20, Т21 (М 1:100)**

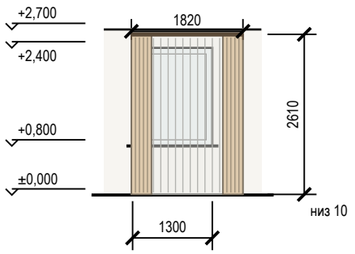


## Карта окон: окно → шина → полотно

| Поз. | Окно, пом. | Проём Ш×В, подоконник | Верх ниши | Изделие | Шина / карниз: длина, крепление | Верх шины | Полотно: длина, низ | Управление |
|---|---|---|---|---|---|---|---|---|
| Т1 | 1, пом. 1 | 1500×1600, подок. 800 | | портьеры | шина, 2500, в нише потолка, вынос 150 | +2,620 | 2610, низ 10 (парит) | вручную |
| Т2 | 1, пом. 1 | 1500×1600, подок. 800 | | тюль | шина, 2500, в нише потолка, вынос 150 | +2,620 | 2610, низ 10 (парит) | вручную |
| Т7 | 1, пом. 3 | 1400×1600, подок. 800 | | портьеры | шина, 1820, в нише потолка, вынос 150 | +2,620 | 2610, низ 10 (парит) | вручную |
| Т8 | 1, пом. 3 | 1400×1600, подок. 800 | | тюль | шина, 1820, в нише потолка, вынос 150 | +2,620 | 2610, низ 10 (парит) | вручную |
| Т13 | 1, пом. 4 | 1000×1400, подок. 1000 | | портьеры | шина, 2250, в нише потолка, вынос 150 | +2,620 | 2610, низ 10 (парит) | вручную |
| Т14 | 1, пом. 4 | 1000×1400, подок. 1000 | | тюль | шина, 2250, в нише потолка, вынос 150 | +2,620 | 2610, низ 10 (парит) | вручную |
| Т15 | 2, пом. 4 | 1400×1600, подок. 900 | | римская штора | карниз, 1400, в нише потолка, вынос 60 | +2,620 | 1620, низ 1000 | шнур, петля низом 1500, натяжитель |
| Т20 | 1, пом. 6 | 1300×1600, подок. 800 | | портьеры | шина, 1820, в нише потолка, вынос 150 | +2,620 | 2610, низ 10 (парит) | вручную |
| Т21 | 1, пом. 6 | 1300×1600, подок. 800 | | тюль | шина, 1820, в нише потолка, вынос 150 | +2,620 | 2610, низ 10 (парит) | вручную |

## Задания смежникам

| Кому | Задание | Пом. |
|---|---|---|
| Электрик | выводы под электрокарнизы не требуются (управление вручную) | |

## Условные обозначения

- портьеры в открытом положении
- римская штора: сложена / опущена
- верх ниши под шторы в потолке
- тюль (на виде окна — прозрачная плашка)
- шина или карниз на отметке верха
- оконный проём

## Примечания

1. Отметки — от чистого пола помещения; размеры — мм. Длины полотен уточняются замером после чистовой отделки пола и потолка, до раскроя.
2. Карнизы — на анкеры по основанию; на ГКЛ — только по закладной.
3. Полотно портьер «парит» над полом на 10 мм; сборка портьер — 2,0, тюля — 2,5 (ширина полотна — в ведомости текстиля).
4. Шнур римской шторы — с натяжителем, петля низом не ниже 1500 мм от пола (защита детей; EN 13120 — рекомендация).
5. Электрокарнизы не предусмотрены; при замене на электропривод — вывод кабеля в нише у края шины (задание электрику).
6. Марки изделий — по плану текстиля и декора (лист 45) и ведомости текстиля (лист 47).

**Допущения и предложения на листе**

Основа листа: размеры сняты с растрового плана заказчика с частичными размерами: рисунок не в масштабе, помещения выровнены по подписанным размерам мебели и проходов; контрольный обмер не выполнен (К-1); высота потолка 2700 мм принята: на плане заказчика её нет (К-2); толщины стен 300 / 120 мм приняты по плану заказчика, не замерены (К-1); разрешённая мощность 15 кВт принята по типовым ТУ для квартиры, ТУ заказчиком не переданы (К-4).
См. лист открытых вопросов (лист 6, записи К-1, К-2, К-4).

| Изм. | Кол.уч | Лист | № док. | Подп. | Дата |
|---|---|---|---|---|---|
| Разраб. | | Кырлан А.С. | | | 18.10.26 |
| Пров. | | | | | |
| ГИП | | | | | |
| | | | | | |
| Н. контр. | | | | | |
| Утв. | | | | | |

**ГД-2026-008-АИ**

Квартира с кабинетом

Общая площадь 127,29* м² · * размеры со скана, не замерены (реестр — л. 6, К-1)

Дизайн-проект интерьера

| Стадия | Лист | Листов |
|---|---|---|
| РП | 46 | 92 |

**Шторы и карнизы**

М б/м

**Кырлан Александр Сергеевич**

# Ведомость текстиля

Шторы, тюль, римские шторы, ковры, подушки и пледы · размеры в мм · марки — по плану текстиля и декора

## Текстиль: шторы, ковры, подушки, пледы

| Поз. | Пом. | Изделие | Размер, мм | Ткань, состав, плотность | Сборка, ширина полотна | | Цвет (система, код) | Кол. | Примечание |
|---|---|---|---|---|---|---|---|---|---|
| T1 | 1 | Портьеры-волна | шина 2500 × полотно 2610 | лён с блэкаут-подкладкой; лён 100 %; 320 г/м² | × 2, ширина 5000 | | NCS S 2010-Y30R (Тёплый льняной беж) | 2 | низ 10 (парит); в нише потолка |
| T2 | 1 | Тюль | шина 2500 × полотно 2610 | вуаль; полиэстер 100 % | × 2,5, ширина 6250 | | Tikkurila V503 (Winter) | 1 | низ 10 (парит); в нише потолка |
| T3 | 1 | Ковёр под кроватью | 2800×1850 | шерсть, ручное ткачество; шерсть 80 %, хлопок 20 % | | | NCS S 5020-G50Y (Оливковый) | 1 | противоскользящая подложка; ворс 10 мм |
| T4 | 1 | Подушки декоративные на кровать | 500×500 | лён 100 % | | | NCS S 2010-Y30R (Тёплый льняной беж) | 3 | на C1 |
| T5 | 1 | Подушки на кровать, акцент | 400×600 | хлопковый бархат 100 % | | | Farrow & Ball No. 34 (Calke Green традиционный шалфей) | 2 | на C1 |
| T6 | 1 | Плед на кровать | 1300×1700 | шерсть мериноса 100 % | | | Farrow & Ball No. 34 (Calke Green традиционный шалфей) | 1 | на C1 |
| T7 | 3 | Портьеры-волна | шина 1820 × полотно 2610 | лён с блэкаут-подкладкой; лён 100 %; 320 г/м² | × 2, ширина 3640 | | NCS S 2010-Y30R (Тёплый льняной беж) | 2 | низ 10 (парит); в нише потолка |
| T8 | 3 | Тюль | шина 1820 × полотно 2610 | вуаль; полиэстер 100 % | × 2,5, ширина 4550 | | Tikkurila V503 (Winter) | 1 | низ 10 (парит); в нише потолка |
| T9 | 3 | Ковёр под кроватью | 2500×1800 | шерсть, плоское плетение; шерсть 100 % | | | Farrow & Ball No. 66 (India Yellow — глубокая горчица) | 1 | противоскользящая подложка; ворс 8 мм |
| T10 | 3 | Подушки декоративные на кровать | 500×500 | букле (шерсть 60 %, полиэстер 40 %) | | | Farrow & Ball No. 286 (Peignoir — серо-розовый) | 3 | на K4 |
| T11 | 3 | Подушки на кровать, акцент | 400×600 | хлопковый бархат 100 % | | | NCS S 5030-B10G (Павлиний сине-зелёный) | 2 | на K4 |
| T12 | 3 | Плед на кровать | 1300×1700 | шерсть мериноса 100 % | | | Farrow & Ball No. 34 (Calke Green традиционный шалфей) | 1 | на K4 |
| T13 | 4 | Портьеры-волна (гостиная) | шина 2250 × полотно 2610 | лён 70 %, вискоза 30 %; 280 г/м² | × 2, ширина 4500 | | NCS S 2010-Y30R (Тёплый льняной беж) | 2 | низ 10 (парит); в нише потолка |
| T14 | 4 | Тюль (гостиная) | шина 2250 × полотно 2610 | вуаль; полиэстер 100 % | × 2,5, ширина 5625 | | Tikkurila V503 (Winter) | 1 | низ 10 (парит); в нише потолка |
| T15 | 4 | Римская штора (кухня) | карниз 1400 × полотно 1620 | лён 100 % | | | Farrow & Ball No. 66 (India Yellow — глубокая горчица) | 1 | низ 1000; в нише потолка; шнур: петля 1500, натяжитель |
| T16 | 4 | Ковёр в зоне отдыха | 3000×1150 | шерсть, петля; шерсть 100 % | | | Farrow & Ball No. 66 (India Yellow — глубокая горчица) | 1 | противоскользящая подложка; ворс низкий |
| T17 | 4 | Подушки на диван | 500×500 | букле (шерсть 60 %, полиэстер 40 %) | | | NCS S 2010-Y30R (Тёплый льняной беж) | 3 | на Kx9 |
| T18 | 4 | Подушки на диван, акцент | 400×600 | хлопковый бархат 100 % | | | Farrow & Ball No. 34 (Calke Green традиционный шалфей) | 2 | на Kx9 |
| T19 | 4 | Плед на диван | 1300×1700 | альпака 50 %, шерсть 50 % | | | Farrow & Ball No. 66 (India Yellow — глубокая горчица) | 1 | на Kx9 |
| T20 | 6 | Портьеры-волна | шина 1820 × полотно 2610 | лён с блэкаут-подкладкой; лён 100 %; 320 г/м² | × 2, ширина 3640 | | NCS S 2010-Y30R (Тёплый льняной беж) | 2 | низ 10 (парит); в нише потолка |
| T21 | 6 | Тюль | шина 1820 × полотно 2610 | вуаль; полиэстер 100 % | × 2,5, ширина 4550 | | Tikkurila V503 (Winter) | 1 | низ 10 (парит); в нише потолка |
| T22 | 6 | Ковёр под кроватью | 2500×1800 | шерсть, плоское плетение; шерсть 100 % | | | Farrow & Ball No. 66 (India Yellow — глубокая горчица) | 1 | противоскользящая подложка; ворс 8 мм |
| T23 | 6 | Подушки декоративные на кровать | 500×500 | букле (шерсть 60 %, полиэстер 40 %) | | | Farrow & Ball No. 286 (Peignoir — серо-розовый) | 3 | на Д2 |
| T24 | 6 | Подушки на кровать, акцент | 400×600 | хлопковый бархат 100 % | | | NCS S 5030-B10G (Павлиний сине-зелёный) | 2 | на Д2 |
| T25 | 6 | Плед на кровать | 1300×1700 | шерсть мериноса 100 % | | | Farrow & Ball No. 34 (Calke Green традиционный шалфей) | 1 | на Д2 |

образец цвета — по HEX производителя краски, справочно

Итого: шторы и тюль — 13 шт.; ковры и дорожки — 4 шт.; подушки, пледы, покрывала — 24 шт.

### Примечания

1. Коды цвета — ориентир подбора по веерам производителей красок; ткань утверждается по образцу при дневном свете и при свете проекта 2700–3000 K.
2. Размеры полотен — по замеру после чистовой отделки пола и потолка; ширина полотна указана с учётом сборки, без припусков на швы. Схемы окон и отметки шин лист 46.
3. Портьеры и тюль — на тесьме «волна» по системе шины; блэкаут — подкладкой. Ковры — на противоскользящей подложке.
4. Замена изделия — аналогом по характеристикам (состав, плотность, размер, цвет по образцу) с согласованием автора проекта.
5. Места изделий — план текстиля и декора (лист 45); подушки и пледы — по марке мебели.

**Допущения и предложения на листе**

Основа листа: размеры сняты с растрового плана заказчика с частичными размерами: рисунок не в масштабе, помещения выровнены по подписанным размерам мебели и проходов; контрольный обмер не выполнен (К-1); высота потолка 2700 мм принята: на плане заказчика её нет (К-2); толщины стен 300 / 120 мм приняты по плану заказчика, не замерены (К-1); разрешённая мощность 15 кВт принята по типовым ТУ для квартиры, ТУ заказчиком не переданы (К-4).

См. лист открытых вопросов (лист 6, записи К-1, К-2, К-4).

| Изм. | Кол.уч | Лист | № док. | Подп. | Дата |
|---|---|---|---|---|---|
| Разраб. | | Кырлан А.С. | | | 18.10.26 |
| Пров. | | | | | |
| ГИП | | | | | |
| | | | | | |
| Н. контр. | | | | | |
| Утв. | | | | | |

**ГД-2026-008-АИ**

Квартира с кабинетом

Общая площадь 127,29* м² · * размеры со скана, не замерены (реестр — л. 6, К-1)

Дизайн-проект интерьера

| Стадия | Лист | Листов |
|---|---|---|
| РП | 47 | 92 |

**Ведомость текстиля**

М б/м

**Кырлан Александр Сергеевич**

# Ведомость декора. Схемы развески

Картины, зеркала, растения, настольный декор · схемы развески (М 1:100) · высоты — мм от чистого пола

## Декор: картины, зеркала, растения, предметы

картина · зеркало · мебель под изделием

| Поз. | Пом. | Предмет | Размер, мм | Место: стена, высота от пола, мм | Масса, кг | Крепёж и основание | Свет места, отделка | Кол. |
|---|---|---|---|---|---|---|---|---|
| ДК1 | 1 | Картина над кроватью | 1200×700 | стена Б, привязка 1400; низ 1300, центр 1650; над С1 | 4 | подвес по основанию, 2 точки | рама — дуб | 1 |
| ДК2 | 6 | Картина над кроватью | 600×700 | стена Б, привязка 1990; низ 1100, центр 1450; над Д2 | 4 | подвес по основанию, 2 точки | рама — дуб | 1 |
| ДК3 | 3 | Картина над диваном | 1400×700 | стена Г, привязка 3275; низ 1000, центр 1350; над К4 | 4 | подвес по основанию, 2 точки | рама — дуб | 1 |
| ДК4 | 3 | Зеркало в рост в тонкой чёрной раме | 600×1600 | стена В, привязка 140; низ 300, центр 1100 | 12 | анкер для пустотелых оснований, 4 шт.; основание: перегородка — определить обмером до монтажа; нагрузка 30 кг | рама — чёрный матовый металл | 1 |
| ДК5 | 6 | Зеркало в рост в тонкой чёрной раме | 600×1600 | стена Б, привязка 840; низ 300, центр 1100 | 12 | анкер для пустотелых оснований, 4 шт.; основание: перегородка — определить обмером до монтажа; нагрузка 30 кг | рама — чёрный матовый металл | 1 |
| ДК6 | 4 | Картина | 1200×900 | стена Г, привязка 800; центр 1550 | 6 | анкер, 2 шт.; основание: перегородка — определить обмером до монтажа; нагрузка 15 кг |  | 1 |
| ДК7 | 4 | Растение | 450×450 | напольное |  |  | свет средний | 1 |
| ДК8 | 4 | Ваза керамическая с ветками на обеденном столе | 200×350 | на М5 |  |  |  | 1 |
| ДК9 | 8 | Зеркало | 800×1800 | стена Б, привязка 190; низ 550, центр 1450 | 18 | анкер, 4 шт.; основание: перегородка — определить обмером до монтажа; нагрузка 40 кг | рама — чёрный матовый металл | 1 |

**ДК1 — Спальня (пом. 1), стена Б (М 1:100)**

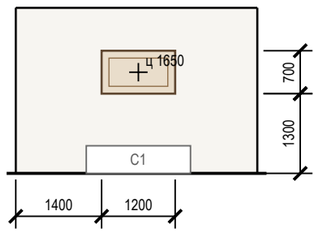


**ДК2 — Детская (пом. 6), стена Б (М 1:100)**

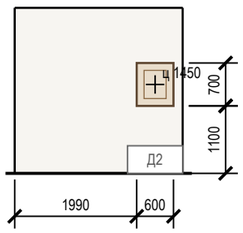


**ДК3 — Кабинет (пом. 3), стена Г (М 1:100)**

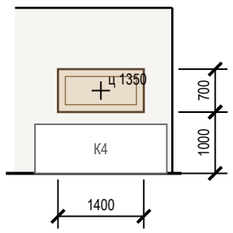


**ДК4 — Кабинет (пом. 3), стена В (М 1:100)**

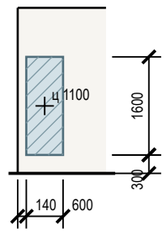


**ДК5 — Детская (пом. 6), стена Б (М 1:100)**

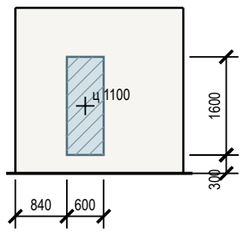


**ДК6 — Кухня-гостиная (пом. 4), стена Г (М 1:100)**

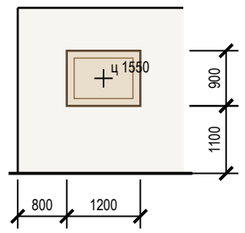


**ДК9 — Прихожая (пом. 8), стена Б (М 1:100)**

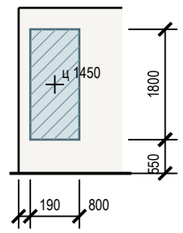


**Допущения и предложения на листе**

Основа листа: размеры сняты с растрового плана заказчика с частичными размерами: рисунок не в масштабе, помещения выровнены по подписанным размерам мебели и проходов; контрольный обмер не выполнен (К-1); высота потолка 2700 мм принята: на плане заказчика её нет (К-2); толщины стен 300 / 120 мм приняты по плану заказчика, не замерены (К-1); разрешённая мощность 15 кВт принята по типовым ТУ для квартиры, ТУ заказчиком не переданы (К-4).

См. лист открытых вопросов (лист 6, записи К-1, К-2, К-4).

## Примечания

1. Высоты — от чистого пола помещения до низа изделия, «ц» — до центра; привязки — от чистовой грани угла стены, мм.
2. Над мебелью низ изделия — на 150–250 мм выше спинки или изголовья; без мебели центр — на 1450–1600 мм от пола.
3. Изделия до 5 кг — на два подвеса по основанию; тяжелее — на анкеры с нагрузкой не меньше двойной массы; на ГКЛ — только по закладной или анкеру для пустотелых оснований.
4. Зеркала в рост — с креплением от опрокидывания; в санузлах — влагостойкие, на клей для зеркал и нейтральный силикон.
5. Места изделий — план текстиля и декора (лист 45).

| Изм. | Кол.уч | Лист | № док. | Подп. | Дата |
|---|---|---|---|---|---|
| Разраб. |  | Кырлан А.С. |  |  | 18.10.26 |
| Пров. |  |  |  |  |  |
| ГИП |  |  |  |  |  |
|  |  |  |  |  |  |
| Н. контр. |  |  |  |  |  |
| Утв. |  |  |  |  |  |

**ГД-2026-008-АИ**

Квартира с кабинетом

Общая площадь 127,29* м² · * размеры со скана, не замерены (реестр — л. 6, К-1)

Дизайн-проект интерьера

| Стадия | Лист | Листов |
|---|---|---|
| РП | 48 | 92 |

**Ведомость декора. Схемы развески**

М б/м

**Кырлан Александр Сергеевич**

выпуск 18.10.2026 № d2d5a25dca · стр. 58 из 129

# Встроенная мебель. Схема расположения

встроенная и корпусная мебель на заказ, кухонный гарнитур · размеры в мм · марки — по ведомости изделий

ПРЕДВАРИТЕЛЬНО · не для производства работ · открыто пунктов: 4 (реестр — л. 6)

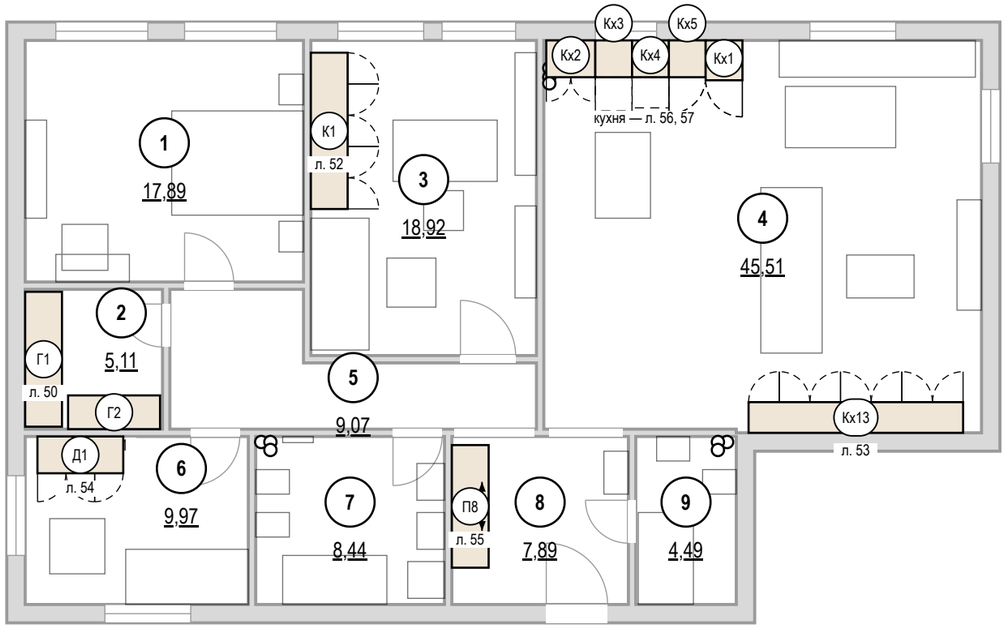


## Ведомость изделий

| Марка | Наименование | Пом. | Ш×Г×В, мм | Лист |
|---|---|---|---|---|
| Г1 | Система хранения | 2 | 2200×600×2400 | 50 |
| Г2 | Система хранения | 2 | 1500×550×2400 | 51 |
| К1 | Шкаф распашной | 3 | 2550×600×2400 | 52 |
| Кх13 | Шкаф распашной | 4 | 3500×500×2400 | 53 |
| Д1 | Шкаф распашной | 6 | 1400×600×2400 | 54 |
| П8 | Шкаф-купе | 8 | 2000×600×2600 | 55 |
| Кх2 | Модуль нижний: мойка | 4 | 800×600×900 | 56 |
| Кх3 | Модуль нижний: ПММ | 4 | 600×600×900 | 56 |
| Кх4 | Модуль нижний: ящики | 4 | 600×600×900 | 56 |
| Кх5 | Пенал: полки | 4 | 600×600×2100 | 56 |
| Кх1 | Пенал: холодильник встр. | 4 | 600×650×2100 | 56 |

## Условные обозначения

- изделие мебельщика: корпус на полу
- навесной модуль (невидимый контур)
- открывание распашного фасада
- зона выдвижения ящика, двери техники
- дверь купе, стрелка — направление движения
- П5 — марка изделия, под ней — лист изделия

## Примечания

1. Изделия — по чистовым размерам помещений; перед раскроем — контрольный замер цеха после чистовой отделки стен, пола и потолка.
2. Открывание фасадов и выдвижение ящиков показано в открытом положении: зоны не пересекают двери, радиаторы, выключатели и проходы.
3. Стояки и счётчики за мебелью — с сервисным люком; газовые трубы мебелью не зашиваются.
4. Покупная мебель — по плану расстановки мебели и спецификации дизайнера; здесь — подложкой.

**Допущения и предложения на листе**

Основа листа: размеры сняты с растрового плана заказчика с частичными размерами: рисунок не в масштабе, помещения выровнены по подписанным размерам мебели и проходов; контрольный обмер не выполнен (К-1); высота потолка 2700 мм принята: на плане заказчика её нет (К-2); толщины стен 300 / 120 мм приняты по плану заказчика, не замерены (К-1); разрешённая мощность 15 кВт принята по типовым ТУ для квартиры, ТУ заказчиком не переданы (К-4).
См. лист открытых вопросов (лист 6, записи К-1, К-2, К-4).

1000 мм · печать 1:1

| Изм. | Кол.уч | Лист | № док. | Подп. | Дата |
|---|---|---|---|---|---|
| Разраб. | | Кырлан А.С. | | | 18.10.26 |
| Пров. | | | | | |
| ГИП | | | | | |
| Н. контр. | | | | | |
| Утв. | | | | | |

**ГД-2026-008-АИ**

Квартира с кабинетом

Общая площадь 127,29* м² · * размеры со скана, не замерены (реестр — л. 6, К-1)

Дизайн-проект интерьера

| Стадия | Лист | Листов |
|---|---|---|
| РП | 49 | 92 |

**Встроенная мебель. Схема расположения**

М 1:100

**Кырлан Александр Сергеевич**

выпуск 18.10.2026 № d2d5a25dca · стр. 59 из 129

# Система хранения Г1

Гардеробная-постирочная (пом. 2) · вид из помещения · размеры в мм, отметки в м

**ПРЕДВАРИТЕЛЬНО · не для производства работ · открыто пунктов: 4 (реестр — л. 6)**

## Общий вид

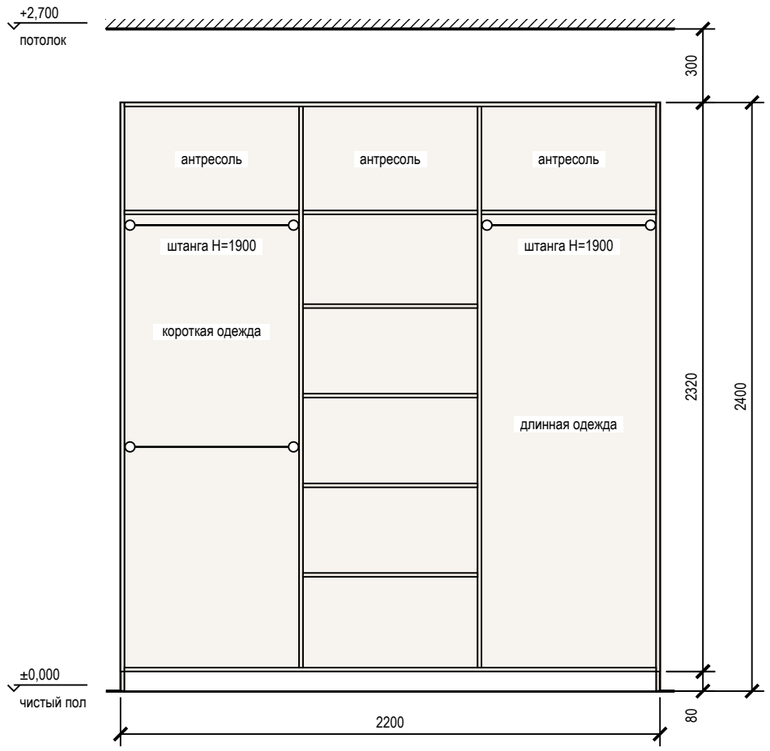


## Наполнение, размеры в свету

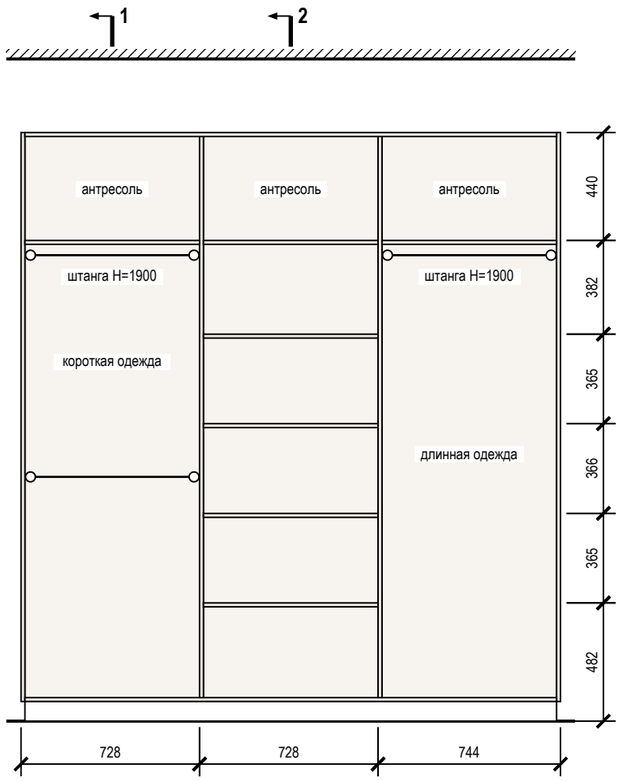


## Разрез 1-1

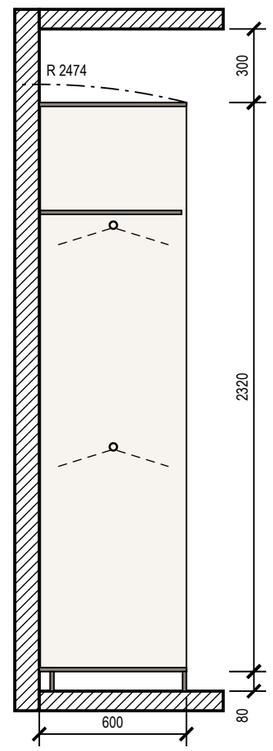


## Разрез 2-2

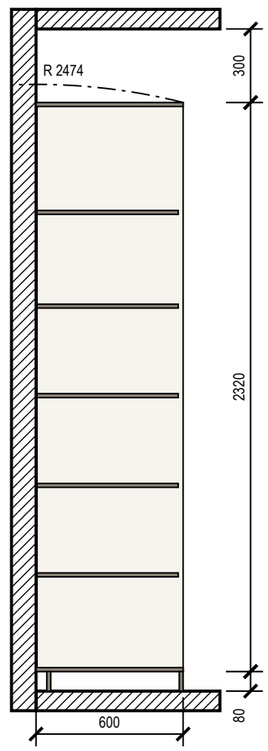


### Примечания

1. Размеры — в мм по чистовой отделке; изделие 2200×600×2400 (Ш×Г×В). Перед раскроем — контрольный замер цеха после чистовой отделки стен, пола и потолка.
2. Корпус — ЛДСП 16 мм, задняя стенка ХДФ 4 мм в паз, цоколь 80 мм на регулируемых опорах; открытая система без фасадов, ящики с фасадами.
3. Кромка: скрытые торцы 0,4 мм, видимые 2 мм (ПВХ/АБС).
4. Номинальные зазоры: между фасадами ящиков 3 мм, фасад ящика — стойка 2 мм.
5. Ящики — направляющие полного выдвижения NL 550 (внутренняя глубина 596 мм ≥ NL + 3); присадка по 32-й системе — выполняет цех.
6. Зазор до потолка 300 мм.
7. Подъём корпуса: диагональ боковины $\sqrt{(2400^2 + 600^2)} = 2474$ мм < 2700 мм до потолка — корпус собирается лёжа и поднимается поворотом.
8. Крепление к стене от опрокидывания: крепление к стене, 3 точки; основание стены и шаг анкеров — монтажная схема шкафов.

### Условные обозначения

- корпус и полки ЛДСП (вид на стену)
- задняя стенка ХДФ
- деталь в разрезе
- штанга для плечиков (на разрезе — плечики 450 мм)
- траектория угла корпуса при подъёме в проектное положение

**Допущения и предложения на листе**

Основа листа: размеры сняты с растрового плана заказчика с частичными размерами: рисунок не в масштабе, помещения выровнены по подписанным размерам мебели и проходов; контрольный обмер не выполнен (К-1); высота потолка 2700 мм принята: на плане заказчика её нет (К-2); толщины стен 300 / 120 мм приняты по плану заказчика, не замерены (К-1); разрешённая мощность 15 кВт принята по типовым ТУ для квартиры, ТУ заказчиком не переданы (К-4).

См. лист открытых вопросов (лист 6, записи К-1, К-2, К-4).

1000 мм · печать 1:1

| Изм. | Кол.уч | Лист | № док. | Подп. | Дата |
|---|---|---|---|---|---|
| Разраб. | | Кырлан А.С. | | | 18.10.26 |
| Пров. | | | | | |
| ГИП | | | | | |
| Н. контр. | | | | | |
| Утв. | | | | | |

**ГД-2026-008-АИ**

Квартира с кабинетом

Общая площадь 127,29* м² · * размеры со скана, не замерены (реестр — л. 6, К-1)

Дизайн-проект интерьера

| Стадия | Лист | Листов |
|---|---|---|
| РП | 50 | 92 |

**Система хранения Г1**

М 1:25

**Кырлан Александр Сергеевич**

выпуск 18.10.2026 · d2d5a25dca · стр. 60 из 129

# Система хранения Г2

Гардеробная-постирочная (пом. 2) · вид из помещения · размеры в мм, отметки в м

**ПРЕДВАРИТЕЛЬНО · не для производства работ · открыто пунктов: 4 (реестр — л. 6)**

## Общий вид

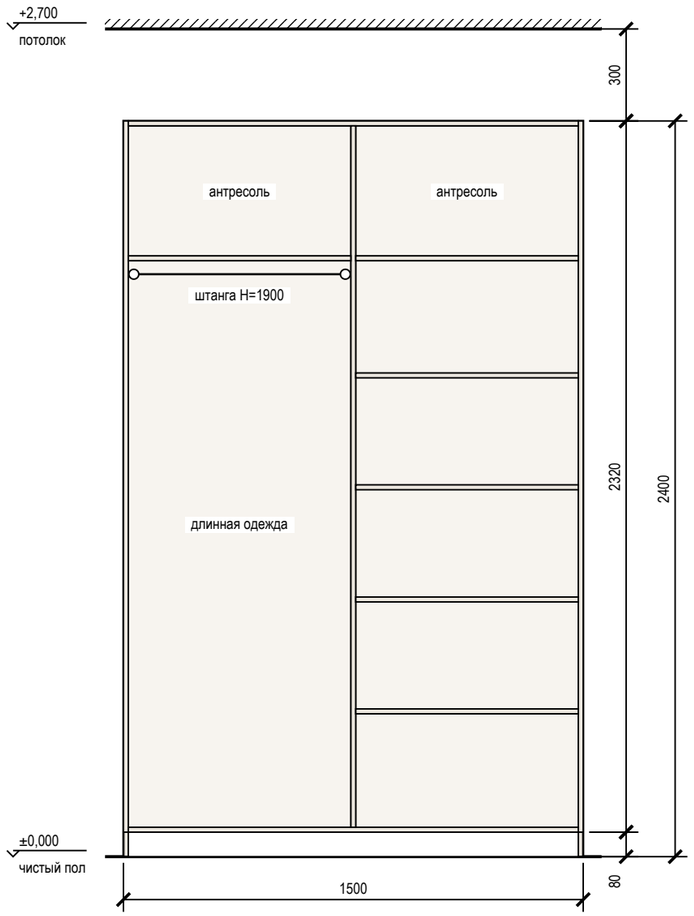


## Наполнение, размеры в свету

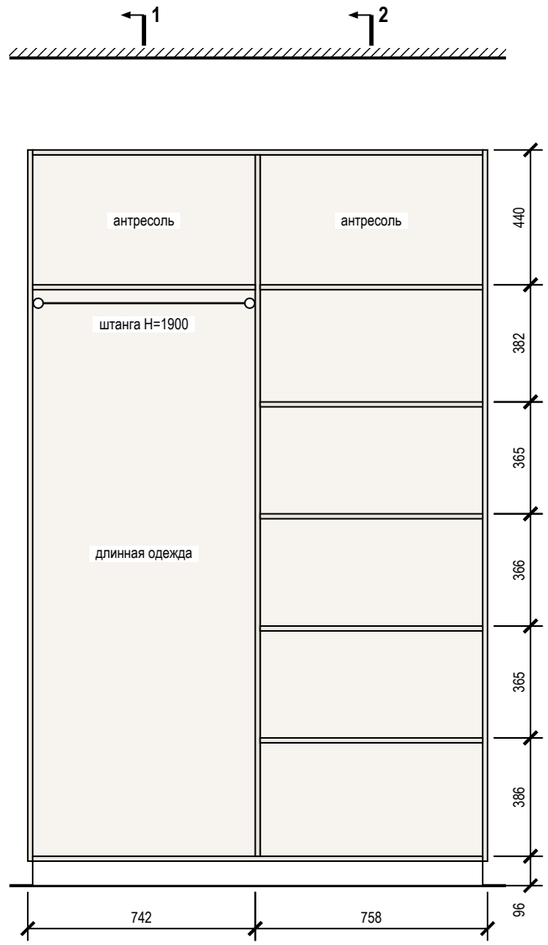


## Разрез 1-1

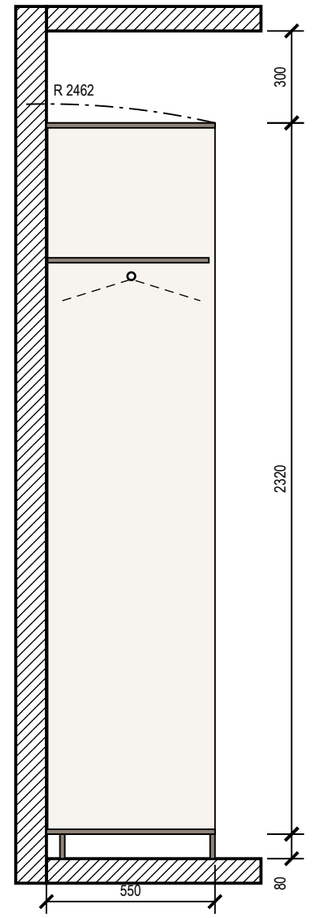


## Разрез 2-2

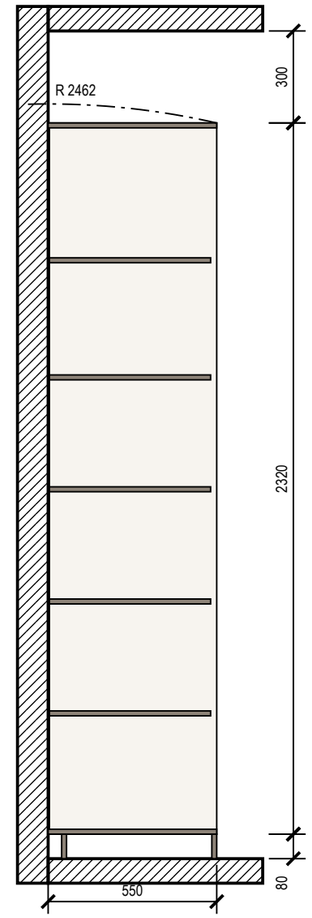


## Примечания

1. Размеры — в мм по чистовой отделке; изделие 1500×550×2400 (Ш×Г×В). Перед раскроем — контрольный замер цеха после чистовой отделки стен, пола и потолка.
2. Корпус — ЛДСП 16 мм, задняя стенка ХДФ 4 мм в паз, цоколь 80 мм на регулируемых опорах; открытая система без фасадов, ящики с фасадами.
3. Кромка: скрытые торцы 0,4 мм, видимые 2 мм (ПВХ/АБС).
4. Номинальные зазоры: между фасадами ящиков 3 мм, фасад ящика — стойка 2 мм.
5. Ящики — направляющие полного выдвижения NL 500 (внутренняя глубина 546 мм ≥ NL + 3); присадка по 32-й системе — выполняет цех.
6. Зазор до потолка 300 мм.
7. Подъём корпуса: диагональ боковины $\sqrt{(2400^2 + 550^2)} = 2462$ мм < 2700 мм до потолка — корпус собирается лёжа и поднимается поворотом.
8. Крепление к стене от опрокидывания: крепление к стене, 3 точки; основание стены и шаг анкеров — монтажная схема шкафов.

## Условные обозначения

- корпус и полки ЛДСП (вид на стену)
- задняя стенка ХДФ
- деталь в разрезе
- штанга для плечиков (на разрезе — плечики 450 мм)
- траектория угла корпуса при подъёме в проектное положение

**Допущения и предложения на листе**

Основа листа: размеры сняты с растрового плана заказчика с частичными размерами: рисунок не в масштабе, помещения выровнены по подписанным размерам мебели и проходов; контрольный обмер не выполнен (К-1); высота потолка 2700 мм принята: на плане заказчика её нет (К-2); толщины стен 300 / 120 мм приняты по плану заказчика, не замерены (К-1); разрешённая мощность 15 кВт принята по типовым ТУ для квартиры, ТУ заказчиком не переданы (К-4).
См. лист открытых вопросов (лист 6, записи К-1, К-2, К-4).

1000 мм · печать 1:1

| | | | | | | | | |
|---|---|---|---|---|---|---|---|---|
| | | | | | | **ГД-2026-008-АИ** | | |
| | | | | | | Квартира с кабинетом<br>Общая площадь 127,29* м² · * размеры со скана, не замерены (реестр — л. 6, К-1) | | |
| Изм. | Кол.уч | Лист | № док. | Подп. | Дата | Дизайн-проект интерьера | Стадия | Лист | Листов |
| Разраб. | | Кырлан А.С. | | | 18.10.26 | | РП | 51 | 92 |
| Пров. | | | | | | | | | |
| ГИП | | | | | | | | | |
| | | | | | | **Система хранения Г2** | **Кырлан Александр Сергеевич** | | |
| Н. контр. | | | | | | М 1:20 | | | |
| Утв. | | | | | | | | | |

выпуск 18.10.2026 № d2d5a25dca · стр. 61 из 129

# Шкаф распашной К1

Кабинет (пом. 3) · вид из помещения · размеры в мм, отметки в м

ПРЕДВАРИТЕЛЬНО · не для производства работ · открыто пунктов: 4 (реестр — л. 6)

**Вид с фасадами**

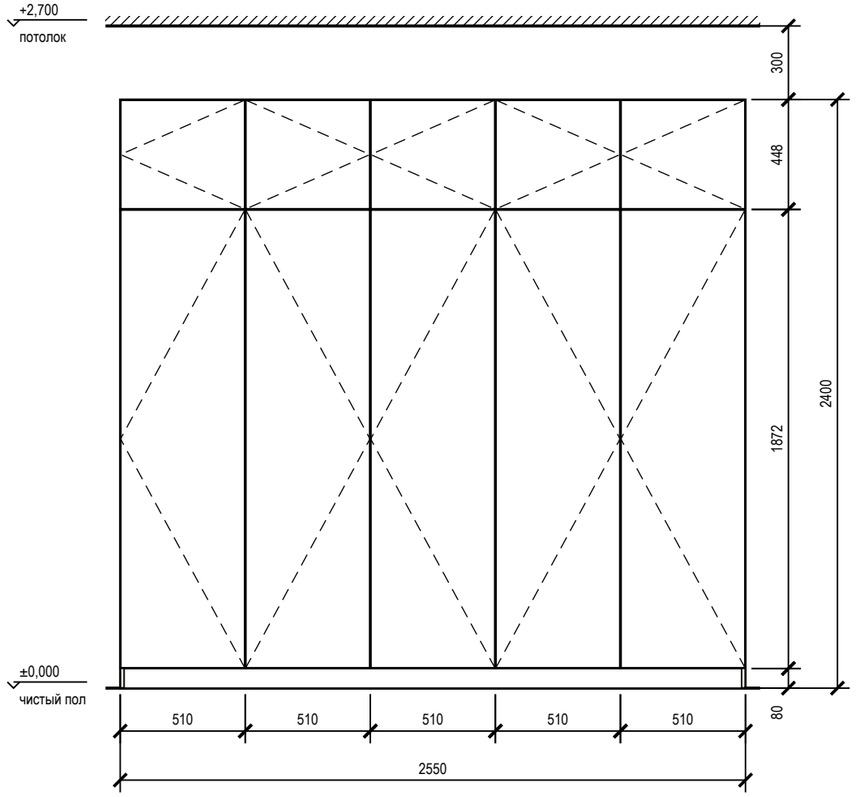


**Вид без фасадов**

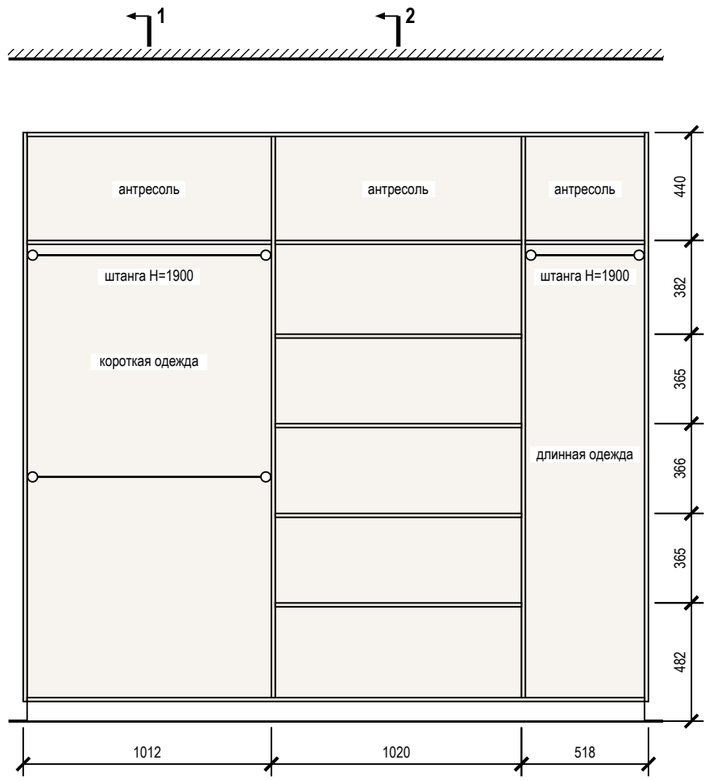


**Разрез 1-1**

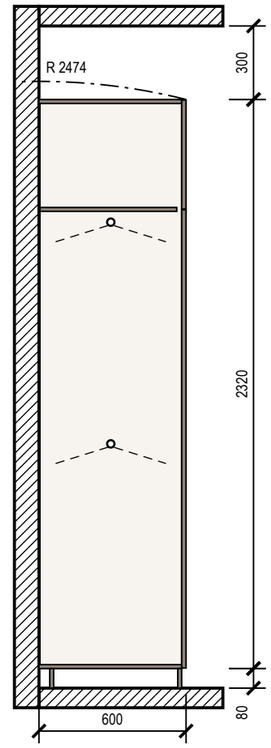


**Разрез 2-2**

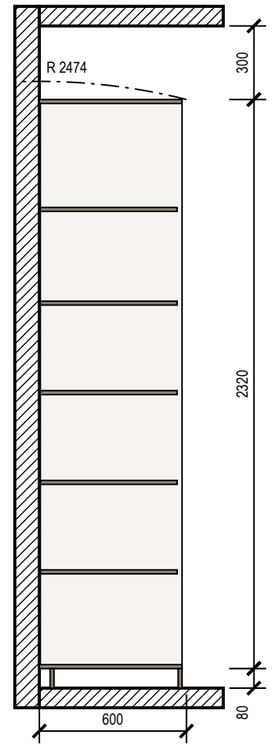


## Примечания

1. Размеры — в мм по чистовой отделке; изделие 2550×600×2400 (Ш×Г×В). Перед раскроем — контрольный замер цеха после чистовой отделки стен, пола и потолка.
2. Корпус — ЛДСП 16 мм, задняя стенка ХДФ 4 мм в паз, цоколь 80 мм на регулируемых опорах; фасады — МДФ, эмаль матовая 18 мм накладные, цвет — по колерной карте; петли с доводчиком: фасад 1869 мм — 4 петли, фасад 445 мм — 2 петли.
3. Кромка: скрытые торцы 0,4 мм, видимые 2 мм (ПВХ/АБС).
4. Номинальные зазоры: между фасадами 3 мм, фасад — стена и фасад — потолок не менее 3 мм, фасад ящика — стойка 2 мм.
5. Ящики — направляющие полного выдвижения NL 550 (внутренняя глубина 578 мм ≥ NL + 3); присадка по 32-й системе — выполняет цех.
6. Зазор до потолка 300 мм.
7. Подъём корпуса: диагональ боковины $\sqrt{(2400^2 + 600^2)} = 2474$ мм < 2700 мм до потолка — корпус собирается лёжа и поднимается поворотом.
8. Крепление к стене от опрокидывания — уголки 2 шт. к несущему основанию (монтажная схема шкафов).

## Условные обозначения

- фасад распашной: линии сходятся к стороне петель
- корпус и полки ЛДСП (вид на стену)
- задняя стенка ХДФ
- деталь в разрезе
- штанга для плечиков (на разрезе — плечики 450 мм)
- траектория угла корпуса при подъёме в проектное положение

**Допущения и предложения на листе**

Основа листа: размеры сняты с растрового плана заказчика с частичными размерами: рисунок не в масштабе, помещения выровнены по подписанным размерам мебели и проходов; контрольный обмер не выполнен (К-1); высота потолка 2700 мм принята: на плане заказчика её нет (К-2); толщины стен 300 / 120 мм приняты по плану заказчика, не замерены (К-1); разрешённая мощность 15 кВт принята по типовым ТУ для квартиры, ТУ заказчиком не переданы (К-4).
См. лист открытых вопросов (лист 6, записи К-1, К-2, К-4).

1000 мм · печать 1:1

| Изм. | Кол.уч | Лист | № док. | Подп. | Дата |
|---|---|---|---|---|---|
| Разраб. | | Кырлан А.С. | | | 18.10.26 |
| Пров. | | | | | |
| ГИП | | | | | |
| Н. контр. | | | | | |
| Утв. | | | | | |

**ГД-2026-008-АИ**

Квартира с кабинетом

Общая площадь 127,29* м² · * размеры со скана, не замерены (реестр — л. 6, К-1)

Дизайн-проект интерьера

| Стадия | Лист | Листов |
|---|---|---|
| РП | 52 | 92 |

**Шкаф распашной К1**

М 1:25

**Кырлан Александр Сергеевич**

выпуск 18.10.2026 · d2d5a25dca · стр. 62 из 129

# Шкаф распашной Кх13

Кухня-гостиная (пом. 4) · вид из помещения · размеры в мм, отметки в м

**ПРЕДВАРИТЕЛЬНО · не для производства работ · открыто пунктов: 4 (реестр — л. 6)**

**Вид с фасадами**

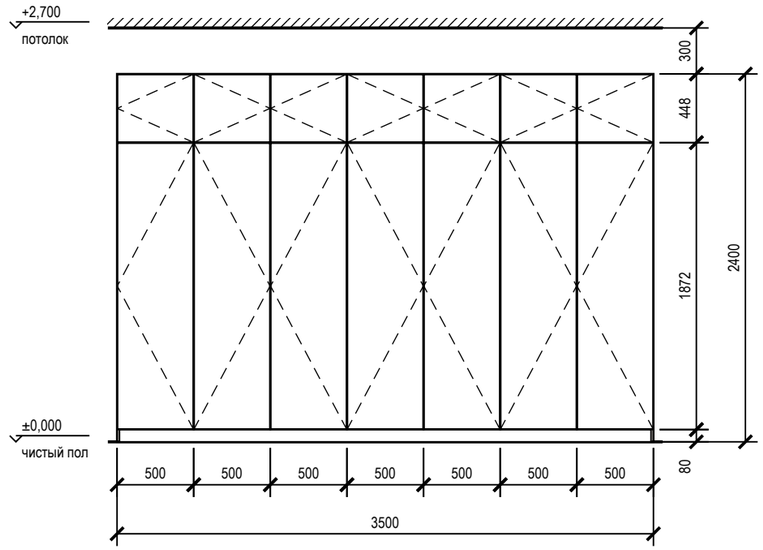


**Вид без фасадов**

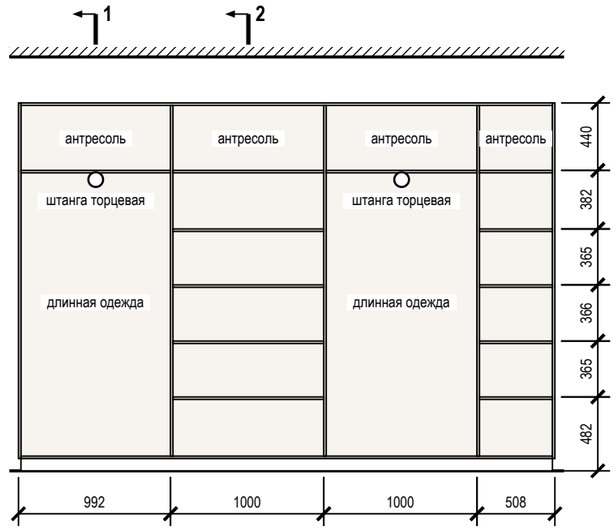


**Разрез 1-1**

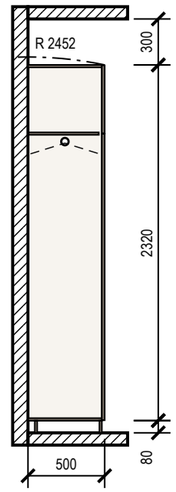


**Разрез 2-2**

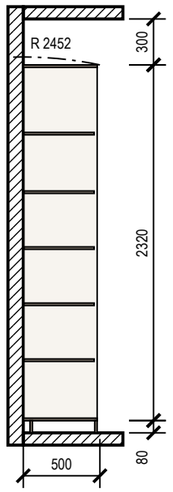


## Примечания

1. Размеры — в мм по чистовой отделке; изделие 3500×500×2400 (Ш×Г×В). Перед раскроем — контрольный замер цеха после чистовой отделки стен, пола и потолка.
2. Корпус — ЛДСП 16 мм, задняя стенка ХДФ 4 мм в паз, цоколь 80 мм на регулируемых опорах; фасады — МДФ, эмаль матовая 18 мм накладные, цвет — по колерной карте; петли с доводчиком: фасад 1869 мм — 4 петли, фасад 445 мм — 2 петли.
3. Кромка: скрытые торцы 0,4 мм, видимые 2 мм (ПВХ/АБС).
4. Номинальные зазоры: между фасадами 3 мм, фасад — стена и фасад — потолок не менее 3 мм, фасад ящика — стойка 2 мм.
5. Ящики — направляющие полного выдвижения NL 450 (внутренняя глубина 478 мм ≥ NL + 3); присадка по 32-й системе — выполняет цех.
6. Зазор до потолка 300 мм.
7. Подъём корпуса: диагональ боковины √(2400² + 500²) = 2452 мм < 2700 мм до потолка — корпус собирается лёжа и поднимается поворотом.
8. Крепление к стене от опрокидывания — уголки 2 шт. к несущему основанию (монтажная схема шкафов).

## Условные обозначения

- фасад распашной: линии сходятся к стороне петель
- корпус и полки ЛДСП (вид на стену)
- задняя стенка ХДФ
- деталь в разрезе
- штанга для плечиков (на разрезе — плечики 450 мм)
- траектория угла корпуса при подъёме в проектное положение

**Допущения и предложения на листе**

Основа листа: размеры сняты с растрового плана заказчика с частичными размерами: рисунок не в масштабе, помещения выровнены по подписанным размерам мебели и проходов; контрольный обмер не выполнен (К-1); высота потолка 2700 мм принята: на плане заказчика её нет (К-2); толщины стен 300 / 120 мм приняты по плану заказчика, не замерены (К-1); разрешённая мощность 15 кВт принята по типовым ТУ для квартиры, ТУ заказчиком не переданы (К-4).
См. лист открытых вопросов (лист 6, записи К-1, К-2, К-4).

1000 мм · печать 1:1

| Изм. | Кол.уч | Лист | № док. | Подп. | Дата |
|---|---|---|---|---|---|
| Разраб. | | Кырлан А.С. | | | 18.10.26 |
| Пров. | | | | | |
| ГИП | | | | | |
| | | | | | |
| Н. контр. | | | | | |
| Утв. | | | | | |

**ГД-2026-008-АИ**

Квартира с кабинетом

Общая площадь 127,29* м² · * размеры со скана, не замерены (реестр — л. 6, К-1)

Дизайн-проект интерьера

| Стадия | Лист | Листов |
|---|---|---|
| РП | 53 | 92 |

**Шкаф распашной Кх13**

М 1:40

**Кырлан Александр Сергеевич**

выпуск 18.10.2026 № d2d5a25dca · стр. 63 из 129

# Шкаф распашной Д1

Детская (пом. 6) · вид из помещения · размеры в мм, отметки в м

**ПРЕДВАРИТЕЛЬНО · не для производства работ · открыто пунктов: 4 (реестр — л. 6)**

### Вид с фасадами

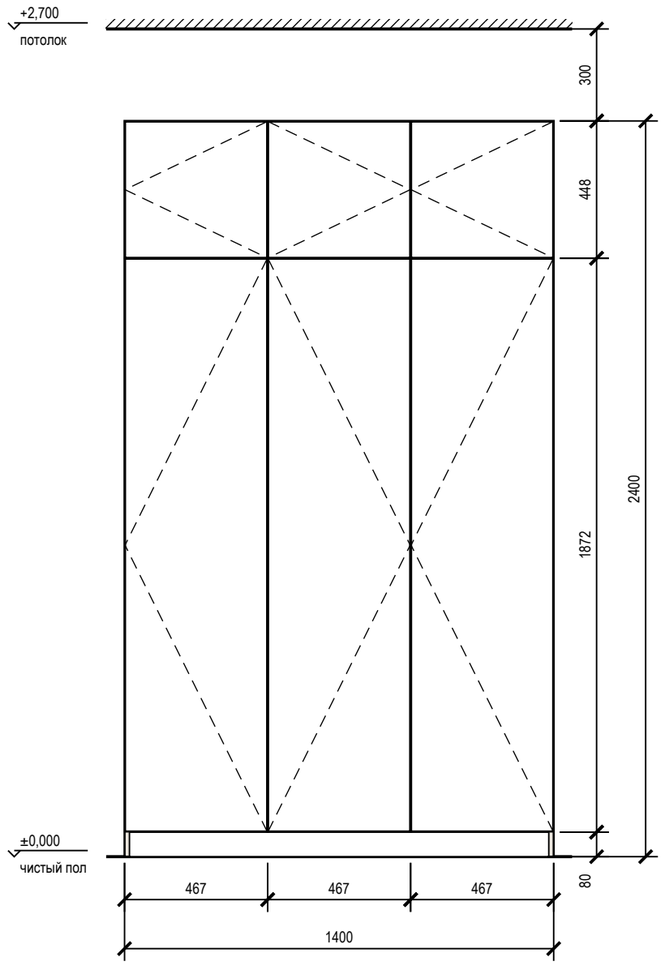


### Вид без фасадов

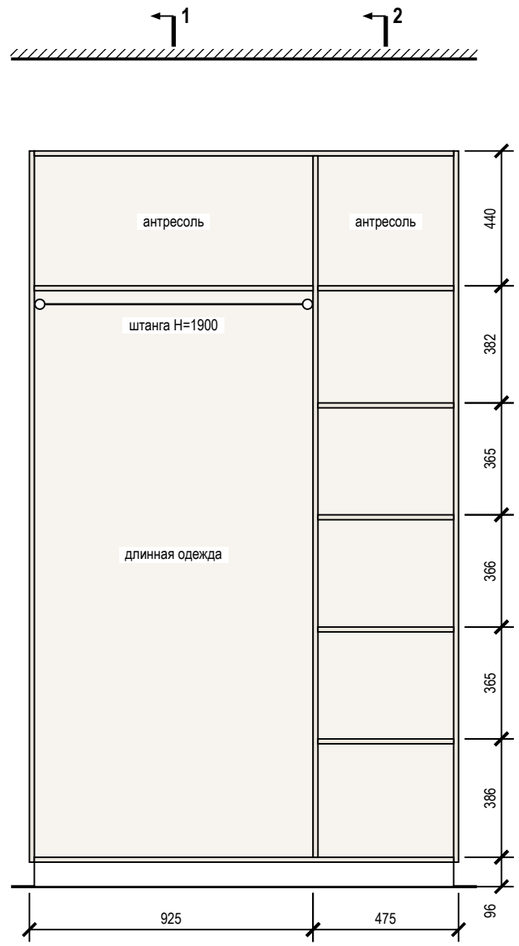


### Разрез 1-1

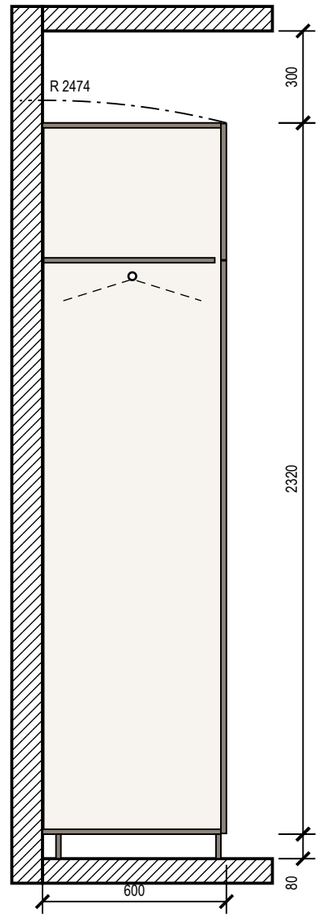


### Разрез 2-2

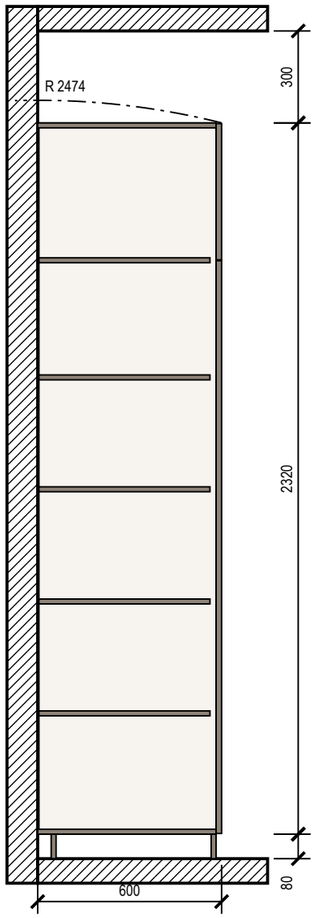


## Примечания

1. Размеры — в мм по чистовой отделке; изделие 1400×600×2400 (Ш×Г×В). Перед раскроем — контрольный замер цеха после чистовой отделки стен, пола и потолка.
2. Корпус — ЛДСП 16 мм, задняя стенка ХДФ 4 мм в паз, цоколь 80 мм на регулируемых опорах; фасады — МДФ, эмаль матовая 18 мм накладные, цвет — по колерной карте; петли с доводчиком: фасад 1869 мм — 4 петли, фасад 445 мм — 2 петли.
3. Кромка: скрытые торцы 0,4 мм, видимые 2 мм (ПВХ/АБС).
4. Номинальные зазоры: между фасадами 3 мм, фасад — стена и фасад — потолок не менее 3 мм, фасад ящика — стойка 2 мм.
5. Ящики — направляющие полного выдвижения NL 550 (внутренняя глубина 578 мм ≥ NL + 3); присадка по 32-й системе — выполняет цех.
6. Зазор до потолка 300 мм.
7. Подъём корпуса: диагональ боковины $\sqrt{(2400^2 + 600^2)}$ = 2474 мм < 2700 мм до потолка — корпус собирается лёжа и поднимается поворотом.
8. Крепление к стене от опрокидывания: крепление к стене, 2 точки; основание стены и шаг анкеров — монтажная схема шкафов.

## Условные обозначения

- фасад распашной: линии сходятся к стороне петель
- корпус и полки ЛДСП (вид на стену)
- задняя стенка ХДФ
- деталь в разрезе
- штанга для плечиков (на разрезе — плечики 450 мм)
- траектория угла корпуса при подъёме в проектное положение

**Допущения и предложения на листе**

Основа листа: размеры сняты с растрового плана заказчика с частичными размерами: рисунок не в масштабе, помещения выровнены по подписанным размерам мебели и проходов; контрольный обмер не выполнен (К-1); высота потолка 2700 мм принята: на плане заказчика её нет (К-2); толщины стен 300 / 120 мм приняты по плану заказчика, не замерены (К-1); разрешённая мощность 15 кВт принята по типовым ТУ для квартиры, ТУ заказчиком не переданы (К-4).
См. лист открытых вопросов (лист 6, записи К-1, К-2, К-4).

1000 мм · печать 1:1

| Изм. | Кол.уч | Лист | № док. | Подп. | Дата |
|---|---|---|---|---|---|
| Разраб. | | Кырлан А.С. | | | 18.10.26 |
| Пров. | | | | | |
| ГИП | | | | | |
| Н. контр. | | | | | |
| Утв. | | | | | |

**ГД-2026-008-АИ**

Квартира с кабинетом

Общая площадь 127,29* м² · * размеры со скана, не замерены (реестр — л. 6, К-1)

Дизайн-проект интерьера

| Стадия | Лист | Листов |
|---|---|---|
| РП | 54 | 92 |

**Шкаф распашной Д1**

М 1:20

**Кырлан Александр Сергеевич**

выпуск 18.10.2026 · d2d5a25dca · стр. 64 из 129

# Шкаф-купе П8

Прихожая (пом. 8) · вид из помещения · размеры в мм, отметки в м

**ПРЕДВАРИТЕЛЬНО · не для производства работ · открыто пунктов: 4 (реестр — л. 6)**

**Вид с фасадами**

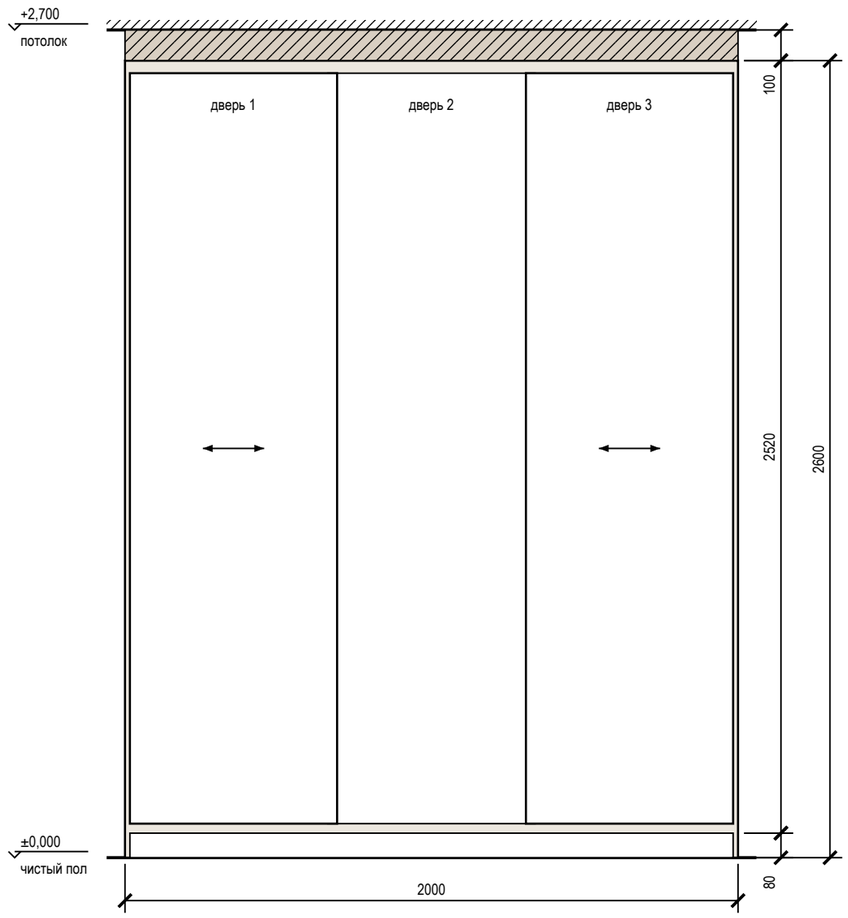


**Вид без фасадов**

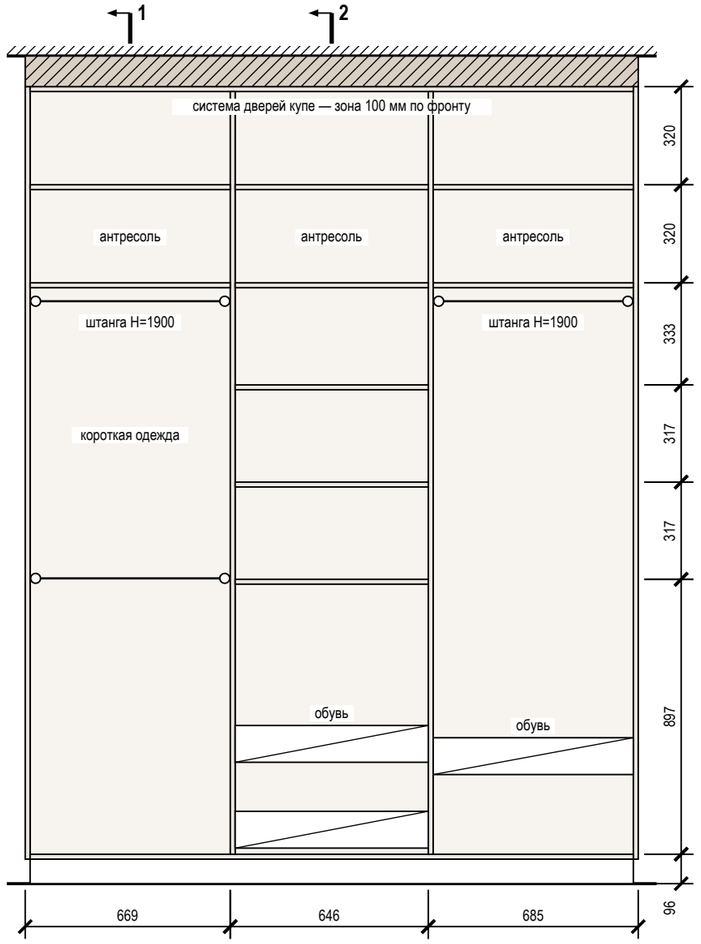


**Разрез 1-1**

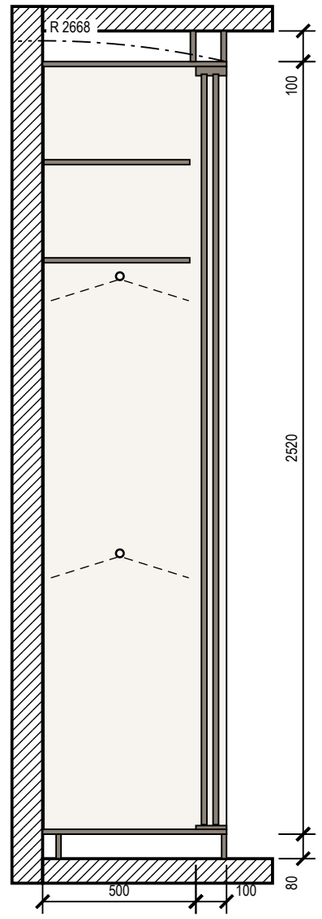


**Разрез 2-2**

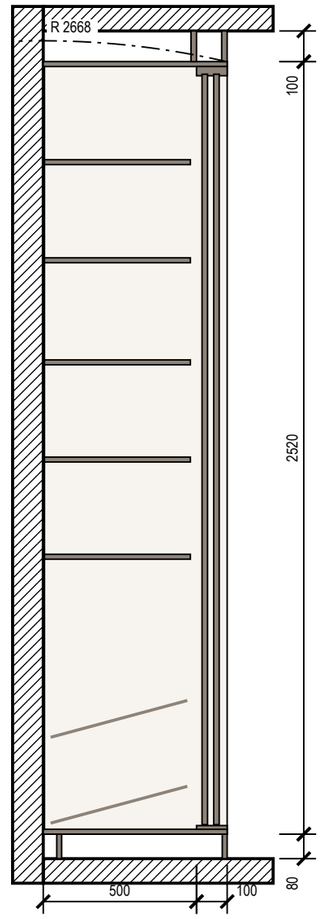


## Примечания

1. Размеры — в мм по чистовой отделке; изделие 2000×600×2600 (Ш×Г×В). Перед раскроем — контрольный замер цеха после чистовой отделки стен, пола и потолка.
2. Корпус — ЛДСП 16 мм, задняя стенка ХДФ 4 мм в паз, цоколь 80 мм на регулируемых опорах; двери купе — ЛДСП 10 мм в алюминиевом профиле, нахлёст 30 мм, ширина двери 676 мм, высота — проём минус 40 мм; цвет — по колерной карте.
3. Кромка: скрытые торцы 0,4 мм, видимые 2 мм (ПВХ/АБС).
4. Номинальные зазоры: дверь купе — боковина 3 мм, фасад ящика — стойка 2 мм; ящики внутри купе — с накладкой 30 мм на стойке со стороны нахлёста дверей.
5. Ящики — направляющие полного выдвижения NL 450 (внутренняя глубина 496 мм ≥ NL + 3); присадка по 32-й системе — выполняет цех.
6. Компенсатор 100 мм — короб из ЛДСП по фронту и торцам, подгоняется к потолку при монтаже (припуск 20 мм), крепится к корпусу и к потолку.
7. Подъём корпуса: диагональ боковины √(2600² + 600²) = 2668 мм < 2700 мм до потолка — корпус собирается лёжа и поднимается поворотом.
8. Крепление к стене от опрокидывания — уголки 2 шт. к несущему основанию (монтажная схема шкафов).

## Условные обозначения

- дверь купе, стрелка — направление движения
- корпус и полки ЛДСП (вид на стену)
- задняя стенка ХДФ
- деталь в разрезе
- компенсатор — короб до потолка
- штанга для плечиков (на разрезе — плечики 450 мм)
- траектория угла корпуса при подъёме в проектное положение

**Допущения и предложения на листе**

Основа листа: размеры сняты с растрового плана заказчика с частичными размерами: рисунок не в масштабе, помещения выровнены по подписанным размерам мебели и проходов; контрольный обмер не выполнен (К-1); высота потолка 2700 мм принята: на плане заказчика её нет (К-2); толщины стен 300 / 120 мм приняты по плану заказчика, не замерены (К-1); разрешённая мощность 15 кВт принята по типовым ТУ для квартиры, ТУ заказчиком не переданы (К-4).
См. лист открытых вопросов (лист 6, записи К-1, К-2, К-4).

1000 мм · печать 1:1

| Изм. | Кол.уч | Лист | № док. | Подп. | Дата |
|---|---|---|---|---|---|
| Разраб. | | Кырлан А.С. | | | 18.10.26 |
| Пров. | | | | | |
| ГИП | | | | | |
| | | | | | |
| Н. контр. | | | | | |
| Утв. | | | | | |

**ГД-2026-008-АИ**

Квартира с кабинетом

Общая площадь 127,29* м² · * размеры со скана, не замерены (реестр — л. 6, К-1)

Дизайн-проект интерьера

| Стадия | Лист | Листов |
|---|---|---|
| РП | 55 | 92 |

**Шкаф-купе П8**

М 1:20

**Кырлан Александр Сергеевич**

выпуск 18.10.2026 № d2d5a25dca · стр. 65 из 129

# Кухня (пом. 4). Развёртка гарнитура

Кухня-гостиная (пом. 4) · стена А · вид из помещения · размеры в мм, отметки в м

## Вид с фасадами

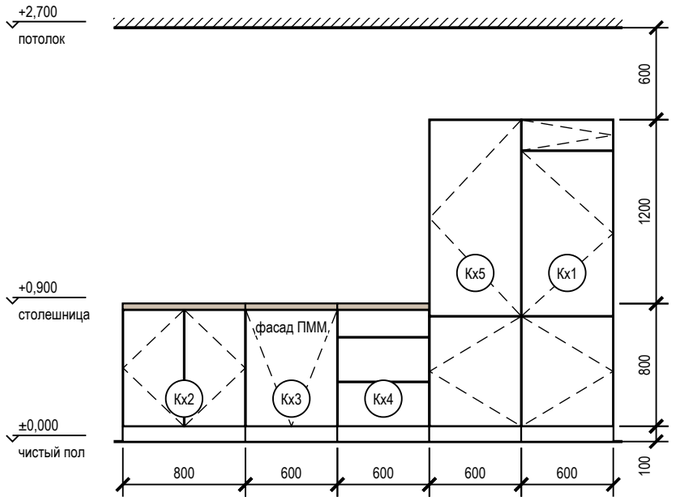


## Вид без фасадов (наполнение, выводы)

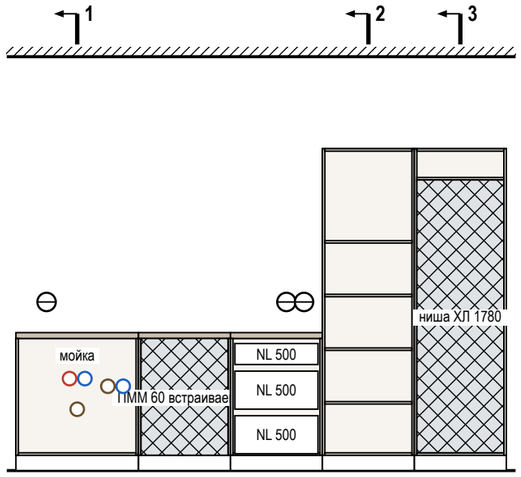


## Разрез 1-1

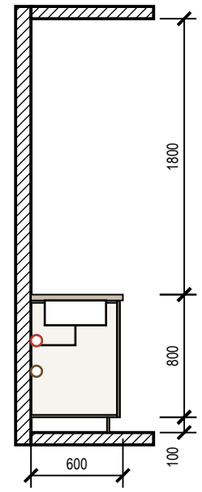


## Разрез 2-2

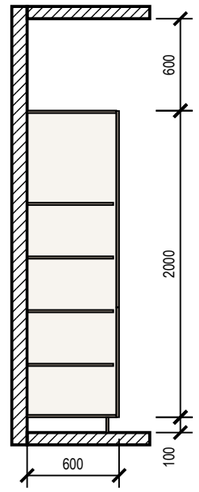


## Разрез 3-3

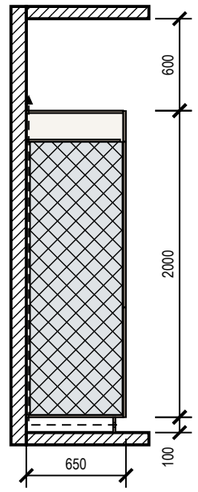


## Условные обозначения

- фасад распашной: линии сходятся к стороне петель
- фасад ящика, карго
- встраиваемая техника
- столешница
- доборная планка
- деталь в разрезе
- К1 — марка модуля
- розетка на стене
- вывод кабеля к технике
- В1 — вывод воды В1 / Т3, канализации К1

## Примечания

1. Размеры — в мм по чистовой отделке, вид из помещения; марки — как на плане расстановки. Перед раскроем — контрольный замер цеха после фартука и пола.
2. Корпуса — ЛДСП 16 мм, задняя стенка ХДФ 4 мм; фасады — МДФ, эмаль матовая 18 мм, цвет по колерной карте; столешница 38 мм, свес 20 мм; цоколь 100 мм.
3. Кромка: скрытые торцы 0,4 мм, видимые 2 мм. Номинальные зазоры: между фасадами 3 мм, фасад — столешница 3 мм, фасад — стена не менее 3 мм.
4. Ящики полного выдвижения и петли — с доводчиком; присадка по 32-й системе — выполняет цех.
5. Ниши техники (холодильник — ориентир 1780 мм) — по монтажным схемам выбранных моделей: решётка в цоколе и канал за пеналом холодильника, зазор за духовым шкафом, фасад ПММ на двери машины.

**Допущения и предложения на листе**

Основа листа: размеры сняты с растрового плана заказчика с частичными размерами: рисунок не в масштабе, помещения выровнены по подписанным размерам мебели и проходов; контрольный обмер не выполнен (К-1); высота потолка 2700 мм принята: на плане заказчика её нет (К-2); толщины стен 300 / 120 мм приняты по плану заказчика, не замерены (К-1); разрешённая мощность 15 кВт принята по типовым ТУ для квартиры, ТУ заказчиком не переданы (К-4).
См. лист открытых вопросов (лист 6, записи К-1, К-2, К-4).

1000 мм · печать 1:1

| Изм. | Кол.уч | Лист | № док. | Подп. | Дата |
|---|---|---|---|---|---|
| Разраб. | | Кырлан А.С. | | | 18.10.26 |
| Пров. | | | | | |
| ГИП | | | | | |
| Н. контр. | | | | | |
| Утв. | | | | | |

**ГД-2026-008-АИ**

Квартира с кабинетом

Общая площадь 127,29* м² · * размеры со скана, не замерены (реестр — л. 6, К-1)

Дизайн-проект интерьера

| Стадия | Лист | Листов |
|---|---|---|
| РП | 56 | 92 |

**Кухня (пом. 4). Развёртка гарнитура**

М 1:40

**Кырлан Александр Сергеевич**

# Кухня (пом. 4). Монтажная схема

Кухня-гостиная (пом. 4) · стена А · размеры в мм от чистых поверхностей, высоты — от чистого пола

**ПРЕДВАРИТЕЛЬНО · не для производства работ · открыто пунктов: 4 (реестр — л. 6)**

## Привязка выводов и крепление модулей

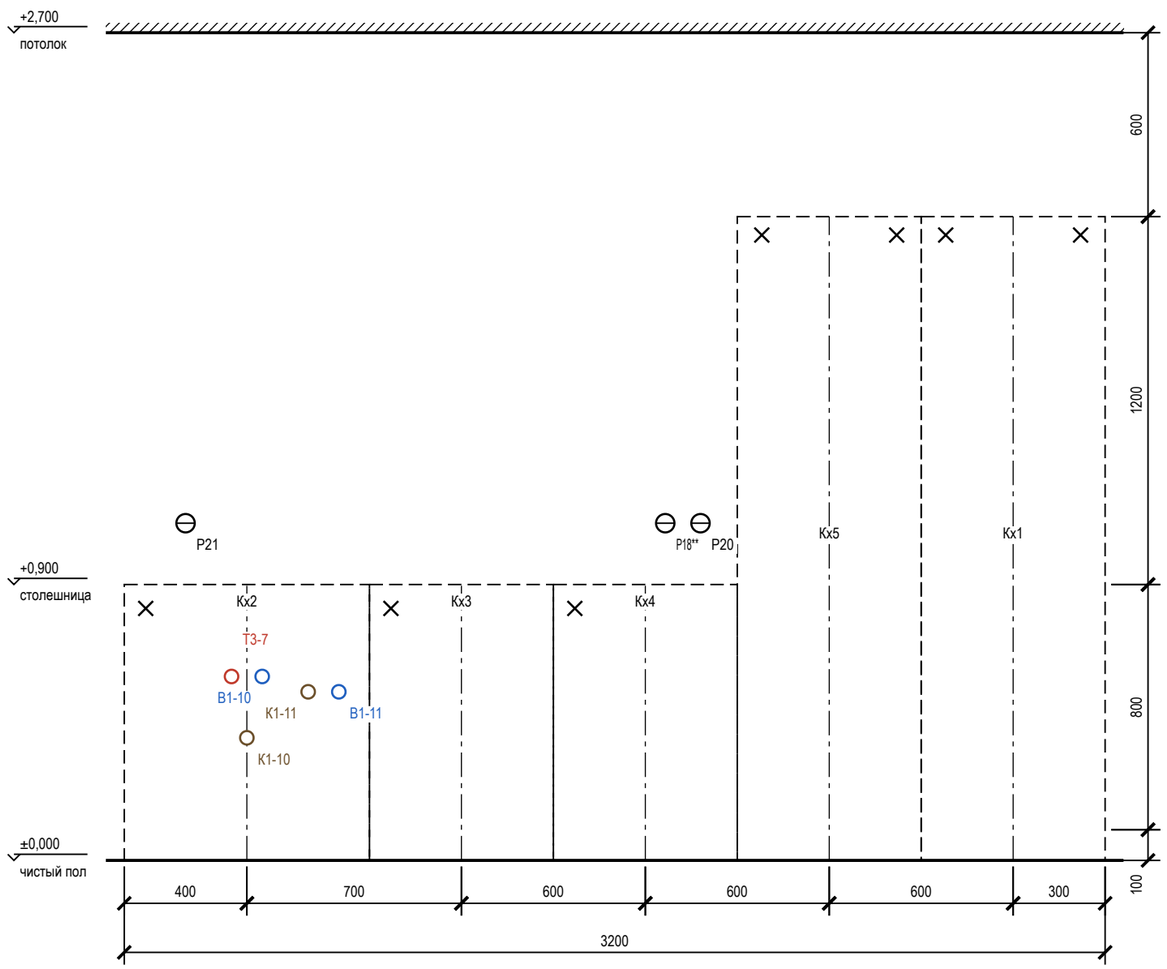


## План столешницы

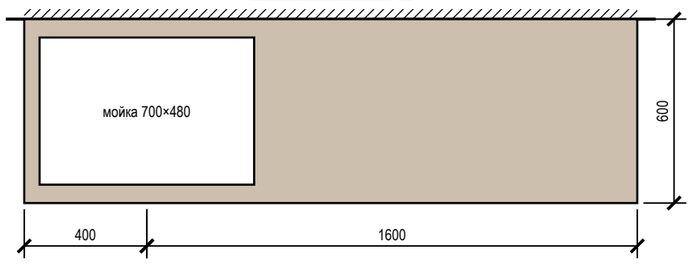


## Привязка выводов к осям модулей

| Код | Назначение | Модуль | От оси, мм | H, мм | Размещение |
|---|---|---|---|---|---|
| P21 | розетка — торшер | Кх2 | −200 | 1100 | над столешницей (фартук) |
| T3-7 | Т3 — межос. 100 | Кх2 | −50 | 600 | в модуле мойки |
| K1-10 | К1 Ø50 — мойка | Кх2 | 0 | 400 | в модуле мойки |
| B1-10 | В1 — межос. 100 | Кх2 | +50 | 600 | в модуле мойки |
| K1-11 | К1 Ø40 — слив ПММ в шкафу мойки | Кх2 | +200 | 550 | в модуле мойки |
| B1-11 | В1 — кран ПММ в шкафу мойки | Кх2 | +300 | 550 | в модуле мойки |
| P18** | розетка ×2 — ТВ (в одной зоне с ТВ1, LAN3) | Кх4 | +65 | 1100 | над столешницей (фартук) |
| P20 | розетка — у ТВ-тумбы | Кх4 | +180 | 1100 | над столешницей (фартук) |

## Зазоры под отделку

| Поверхность | Отделка | Зазор, мм | Учесть |
|---|---|---|---|
| фартук | керамогранит | 10 | от чернового основания до корпуса навесных и столешницы |
| стены | окраска | 5 | под штукатурку и шпаклёвку за пеналом |
| пол | инженерная доска | | цоколь — после укладки пола, опоры ±20 мм |

## Условные обозначения

- навесной модуль (невидимый контур)
- ось модуля (от неё — привязка вывода)
- анкер / уголок крепления к стене
- розетка на стене
- вывод кабеля к технике
- B1 — вывод воды В1 / Т3, канализации К1

**Допущения и предложения на листе**

Основа листа: размеры сняты с растрового плана заказчика с частичными размерами: рисунок не в масштабе, помещения выровнены по подписанным размерам мебели и проходов; контрольный обмер не выполнен (К-1); высота потолка 2700 мм принята: на плане заказчика её нет (К-2); толщины стен 300 / 120 мм приняты по плану заказчика, не замерены (К-1); разрешённая мощность 15 кВт принята по типовым ТУ для квартиры, ТУ заказчиком не переданы (К-4).

Знак «**» — предложение проектировщика, заказчиком не утверждено (согласовать с заказчиком): записи в реестре нет: P18 — высота 1100 мм выше нормы 1 м (ПУЭ 6.6.30) по назначению: питание ТВ, в одной зоне с выводами ТВ1 и LAN3.

См. лист открытых вопросов (лист 6, записи К-1, К-2, К-4).

## Примечания

1. Выводы — по проекту электрики и ВК; привязка по горизонтали — от оси модуля (плюс — вправо по виду), по высоте — от чистого пола до оси вывода.
2. Пенал — уголки к стене 2 шт. сверху; нижние модули — стяжками между собой и уголком к стене; ряд выставить по уровню опорами цоколя.
3. Розетки над столешницей — не ниже 150 мм над ней и не за корпусом техники; розетка за ПММ, духовым шкафом и холодильником — только в соседнем модуле или в зоне цоколя с доступом.
4. Столешница — вырезы по шаблонам выбранных моделей мойки и варочной панели; торцы у стены — герметик, пристеночный плинтус.

1000 мм · печать 1:1

| Изм. | Кол.уч | Лист | № док. | Подп. | Дата |
|---|---|---|---|---|---|
| Разраб. | | Кырлан А.С. | | | 18.10.26 |
| Пров. | | | | | |
| ГИП | | | | | |
| Н. контр. | | | | | |
| Утв. | | | | | |

**ГД-2026-008-АИ**

Квартира с кабинетом

Общая площадь 127,29* м² · * размеры со скана, не замерены (реестр — л. 6, К-1)

Дизайн-проект интерьера

| Стадия | Лист | Листов |
|---|---|---|
| РП | 57 | 92 |

**Кухня (пом. 4). Монтажная схема**

М 1:20

**Кырлан Александр Сергеевич**

выпуск 18.10.2026 № d2d5a25dca · стр. 67 из 129

# Шкафы. Монтажная схема. Лист 1 из 2

крепление к стене, установочные размеры, зазоры под отделку · размеры в мм

**ПРЕДВАРИТЕЛЬНО · не для производства работ · открыто пунктов: 4 (реестр — л. 6)**

**Система хранения Г1 (пом. 2)**

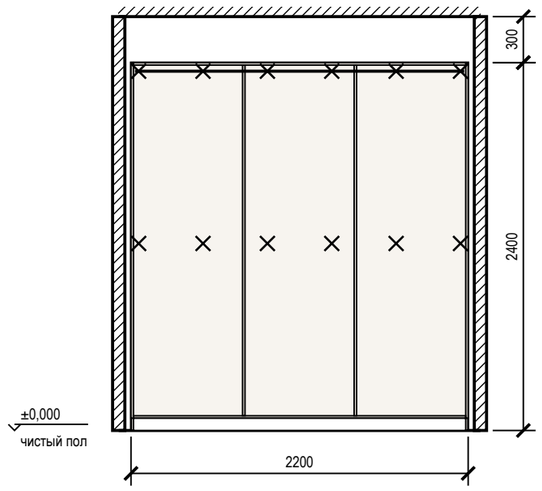


**Система хранения Г2 (пом. 2)**

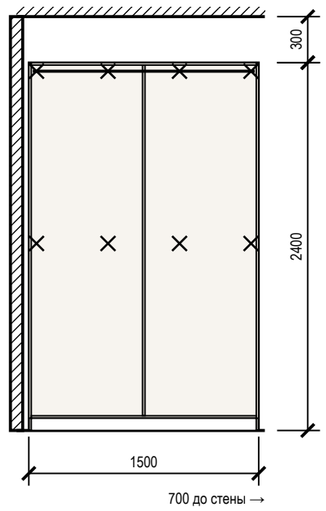


**Шкаф распашной К1 (пом. 3)**

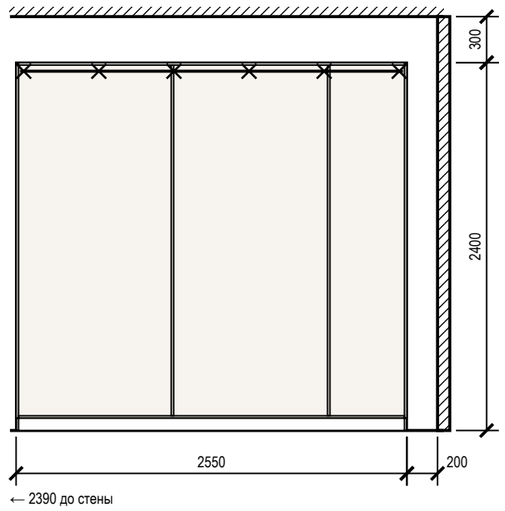


## Крепление и зазоры под отделку (изделия листа 1)

| Марка | Помещение, стена | Основание | Отделка стены | Зазор, мм | Крепёж по планке | От опрокидывания |
|---|---|---|---|---|---|---|
| Г1 | Гардеробная-постирочная (2), стена Г | по основанию — см. таблицу крепежа | окраска | 5 | анкер 12 шт. (2 ряда) | крепление к стене, 3 точки |
| Г2 | Гардеробная-постирочная (2), стена В | по основанию — см. таблицу крепежа | окраска | 5 | анкер 8 шт. (2 ряда) | крепление к стене, 3 точки |
| К1 | Кабинет (3), стена Г | по основанию — см. таблицу крепежа | окраска | 5 | анкер 6 шт., шаг 490 | уголки 2 шт. |

## Крепёж по основанию стены

| Основание стены | Крепёж |
|---|---|
| бетон, ж/б | анкер-шуруп 7,5×72 или дюбель 8×60 с шурупом 5×70 |
| кирпич полнотелый | дюбель 8×80 с шурупом 5×90 |
| газобетон, пазогребень | дюбель для газобетона 10×100 или химический анкер |
| гипсокартон | закладная до обшивки (брус 40×80 или фанера 18 мм), саморез в закладную |

## Условные обозначения

- анкер / уголок крепления к стене
- корпус и полки ЛДСП (вид на стену)
- компенсатор — короб до потолка

## Примечания

1. Установочные размеры — от чистого пола и чистых стен; перед установкой контрольный замер после отделки.
2. Порядок: корпус выставить по уровню опорами цоколя → закрепить к стене по задней планке → навесить двери и фасады, отрегулировать зазоры → подогнать и закрепить компенсатор.
3. Анкеры — с шагом не более 500 мм, не ближе 50 мм от края планки; на ГКЛ только в закладную, установленную до обшивки.
4. Скрытые коммуникации под анкеры проверить детектором; трассы электрики по плану розеток.
5. Монтажная схема на 2 листах, лист 1 из 2; продолжение — на следующем листе схемы. Условные обозначения, таблица крепежа по основанию и примечания повторены на каждом листе.

**Допущения и предложения на листе**

Основа листа: размеры сняты с растрового плана заказчика с частичными размерами: рисунок не в масштабе, помещения выровнены по подписанным размерам мебели и проходов; контрольный обмер не выполнен (К-1); высота потолка 2700 мм принята: на плане заказчика её нет (К-2); толщины стен 300 / 120 мм приняты по плану заказчика, не замерены (К-1); разрешённая мощность 15 кВт принята по типовым ТУ для квартиры, ТУ заказчиком не переданы (К-4).

См. лист открытых вопросов (лист 6, записи К-1, К-2, К-4).

1000 мм · печать 1:1

| Изм. | Кол.уч | Лист | № док. | Подп. | Дата |
|---|---|---|---|---|---|
| Разраб. | | Кырлан А.С. | | | 18.10.26 |
| Пров. | | | | | |
| ГИП | | | | | |
| | | | | | |
| Н. контр. | | | | | |
| Утв. | | | | | |

**ГД-2026-008-АИ**

Квартира с кабинетом

Общая площадь 127,29* м² · * размеры со скана, не замерены (реестр — л. 6, К-1)

Дизайн-проект интерьера

| Стадия | Лист | Листов |
|---|---|---|
| РП | 58 | 92 |

**Шкафы. Монтажная схема. Лист 1 из 2**

М 1:40

**Кырлан Александр Сергеевич**

выпуск 18.10.2026 № d2d5a25dca · стр. 68 из 129

# Шкафы. Монтажная схема. Лист 2 из 2

крепление к стене, установочные размеры, зазоры под отделку · размеры в мм

**ПРЕДВАРИТЕЛЬНО · не для производства работ · открыто пунктов: 4 (реестр — л. 6)**

**Шкаф распашной Кх13 (пом. 4)**

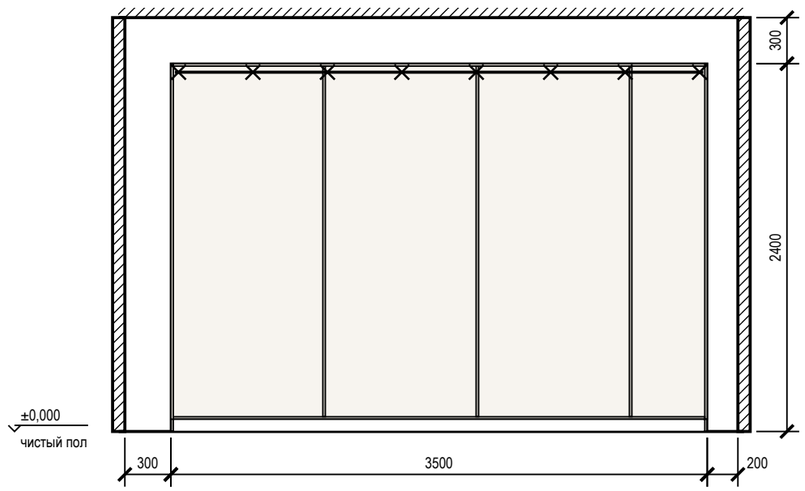


**Шкаф распашной Д1 (пом. 6)**

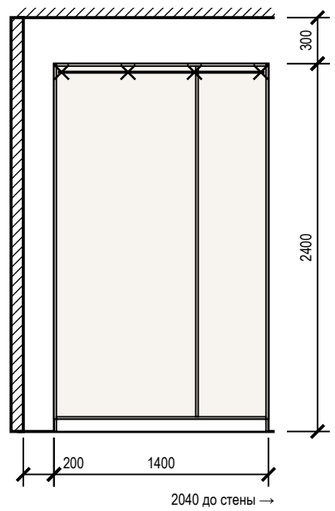


**Шкаф-купе П8 (пом. 8)**

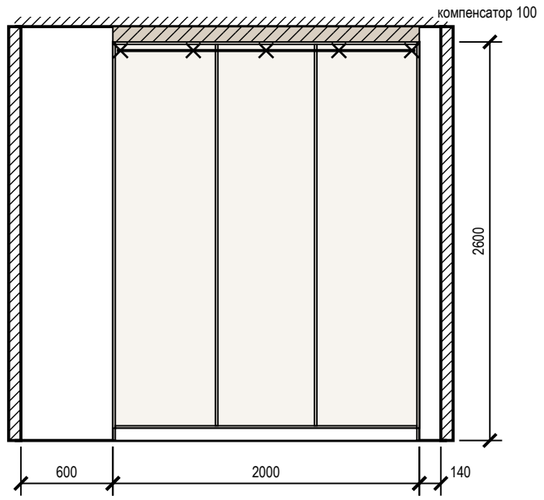


## Крепление и зазоры под отделку (изделия листа 2)

| Марка | Помещение, стена | Основание | Отделка стены | Зазор, мм | Крепёж по планке | От опрокидывания |
|---|---|---|---|---|---|---|
| Кх13 | Кухня-гостиная (4), стена В | по основанию — см. таблицу крепежа | окраска | 5 | анкер 8 шт., шаг 486 | уголки 2 шт. |
| Д1 | Детская (6), стена А | по основанию — см. таблицу крепежа | окраска | 5 | анкер 4 шт., шаг 433 | крепление к стене, 2 точки |
| П8 | Прихожая (8), стена Г | по основанию — см. таблицу крепежа | окраска | 5 | анкер 5 шт., шаг 475 | уголки 2 шт. |

## Крепёж по основанию стены

| Основание стены | Крепёж |
|---|---|
| бетон, ж/б | анкер-шуруп 7,5×72 или дюбель 8×60 с шурупом 5×70 |
| кирпич полнотелый | дюбель 8×80 с шурупом 5×90 |
| газобетон, пазогребень | дюбель для газобетона 10×100 или химический анкер |
| гипсокартон | закладная до обшивки (брус 40×80 или фанера 18 мм), саморез в закладную |

## Условные обозначения

- анкер / уголок крепления к стене
- корпус и полки ЛДСП (вид на стену)
- компенсатор — короб до потолка

## Примечания

1. Установочные размеры — от чистого пола и чистых стен; перед установкой контрольный замер после отделки.
2. Порядок: корпус выставить по уровню опорами цоколя → закрепить к стене по задней планке → навесить двери и фасады, отрегулировать зазоры → подогнать и закрепить компенсатор.
3. Анкеры — с шагом не более 500 мм, не ближе 50 мм от края планки; на ГКЛ только в закладную, установленную до обшивки.
4. Скрытые коммуникации под анкеры проверить детектором; трассы электрики по плану розеток.
5. Монтажная схема на 2 листах, лист 2 из 2. Условные обозначения, таблица крепежа по основанию и примечания повторены на каждом листе.

**Допущения и предложения на листе**

Основа листа: размеры сняты с растрового плана заказчика с частичными размерами: рисунок не в масштабе, помещения выровнены по подписанным размерам мебели и проходов; контрольный обмер не выполнен (К-1); высота потолка 2700 мм принята: на плане заказчика её нет (К-2); толщины стен 300 / 120 мм приняты по плану заказчика, не замерены (К-1); разрешённая мощность 15 кВт принята по типовым ТУ для квартиры, ТУ заказчиком не переданы (К-4).

См. лист открытых вопросов (лист 6, записи К-1, К-2, К-4).

1000 мм · печать 1:1

| Изм. | Кол.уч | Лист | № док. | Подп. | Дата |
|---|---|---|---|---|---|
| Разраб. | | Кырлан А.С. | | | 18.10.26 |
| Пров. | | | | | |
| ГИП | | | | | |
| | | | | | |
| Н. контр. | | | | | |
| Утв. | | | | | |

**ГД-2026-008-АИ**

Квартира с кабинетом

Общая площадь 127,29* м² · * размеры со скана, не замерены (реестр — л. 6, К-1)

| Дизайн-проект интерьера | Стадия | Лист | Листов |
|---|---|---|---|
| | РП | 59 | 92 |

**Шкафы. Монтажная схема. Лист 2 из 2**

М 1:40

**Кырлан Александр Сергеевич**

выпуск 18.10.2026 № d2d5a25dca · стр. 69 из 129

# Ведомости изделий, техники и фурнитуры

встроенная мебель и кухонный гарнитур · размеры в мм

**ПРЕДВАРИТЕЛЬНО · не для производства работ · открыто пунктов: 4 (реестр — л. 6)**

## Ведомость изделий

| Марка | Наименование | Пом. | Ш×Г×В, мм | Корпус | Фасад | Кромка, мм скр./вид. | Кол. |
|---|---|---|---|---|---|---|---|
| Г1 | Система хранения | 2 | 2200×600×2400 | ЛДСП 16 | без фасадов; ящики — МДФ 18, эмаль матовая | 0,4 / 2 | 1 |
| Г2 | Система хранения | 2 | 1500×550×2400 | ЛДСП 16 | без фасадов; ящики — МДФ 18, эмаль матовая | 0,4 / 2 | 1 |
| К1 | Шкаф распашной | 3 | 2550×600×2400 | ЛДСП 16 | МДФ 18, эмаль матовая | 0,4 / 2 | 1 |
| Кх13 | Шкаф распашной | 4 | 3500×500×2400 | ЛДСП 16 | МДФ 18, эмаль матовая | 0,4 / 2 | 1 |
| Д1 | Шкаф распашной | 6 | 1400×600×2400 | ЛДСП 16 | МДФ 18, эмаль матовая | 0,4 / 2 | 1 |
| П8 | Шкаф-купе | 8 | 2000×600×2600 | ЛДСП 16 | рифлёные панели МДФ в алюминиевом профиле | 0,4 / 2 | 1 |
| Кх2 | Модуль нижний: мойка | 4 | 800×600×900 | ЛДСП 16 | МДФ 18, эмаль матовая | 0,4 / 2 | 1 |
| Кх3 | Модуль нижний: ПММ | 4 | 600×600×900 | ЛДСП 16 | МДФ 18, эмаль матовая | 0,4 / 2 | 1 |
| Кх4 | Модуль нижний: ящики | 4 | 600×600×900 | ЛДСП 16 | МДФ 18, эмаль матовая | 0,4 / 2 | 1 |
| Кх5 | Пенал: полки | 4 | 600×600×2100 | ЛДСП 16 | МДФ 18, эмаль матовая | 0,4 / 2 | 1 |
| Кх1 | Пенал: холодильник встр. | 4 | 600×650×2100 | ЛДСП 16 | МДФ 18, эмаль матовая | 0,4 / 2 | 1 |

## Ведомость встраиваемой техники

| Поз. | Прибор | Ниша, вырез, мм | Вентиляция | Питание | Схема |
|---|---|---|---|---|---|
| Кх2 | Мойка врезная / подстольная с сифоном | вырез по шаблону, ориентир 700 × 480 | | смеситель — выводы ВК | по модели |
| Кх3 | Посудомоечная машина встраиваемая, 60 см | ниша 600 × 862 (от пола до низа столешницы) | зазор в цоколе, по схеме | розетка в соседнем модуле | по модели |
| Кх1 | Холодильник встраиваемый, ниша 1780 | ниша 1780 × 560 × 550 | решётка в цоколе, канал за корпусом, выход сверху | розетка над нишей или в соседнем модуле | по модели |

## Ведомость фурнитуры

| № | Фурнитура | Тип, размер | Изделия | Кол. |
|---|---|---|---|---|
| 1 | Полкодержатель с фиксацией | ø5 мм | Г1, Г2, К1, Кх13, Д1, П8, Кх5, Кх1 | 208 |
| 2 | Штанга овальная 30×15, L = 712 | + 2 держателя | Г1 | 3 |
| 3 | Опора регулируемая с цоколем на клипсах | ход 20 мм | Г1, Г2, К1, Кх13, Д1, П8 | 50 |
| 4 | Анкер по основанию стены | по таблице крепежа | Г1, Г2, К1, Кх13, Д1, П8 | 43 |
| 5 | Уголок крепления к стене от опрокидывания | стальной | Г1, Г2, К1, Кх13, Д1, П8, Кх5, Кх1 | 16 |
| 6 | Штанга овальная 30×15, L = 726 | + 2 держателя | Г2 | 1 |
| 7 | Петля накладная 110° с доводчиком | чашка 35 мм | К1, Кх13, Д1, Кх2, Кх5, Кх1 | 106 |
| 8 | Штанга овальная 30×15, L = 996 | + 2 держателя | К1 | 2 |
| 9 | Штанга овальная 30×15, L = 486 | + 2 держателя | К1 | 1 |
| 10 | Штанга выдвижная торцевая | L по глубине | Кх13 | 2 |
| 11 | Штанга овальная 30×15, L = 909 | + 2 держателя | Д1 | 1 |
| 12 | Система дверей купе: профиль, направляющие, ролики | на 3 двери | П8 | 1 |
| 13 | Ручка-профиль вертикальная | в цвет профиля | П8 | 3 |
| 14 | Штанга овальная 30×15, L = 653 | + 2 держателя | П8 | 3 |
| 15 | Полка для обуви выдвижная наклонная | ширина 630 | П8 | 2 |
| 16 | Полка для обуви выдвижная наклонная | ширина 653 | П8 | 1 |
| 17 | Ручка-профиль | латунь матовая | Кх2, Кх3, Кх4, Кх5, Кх1 | 11 |
| 18 | Опора кухонная регулируемая 100–120 мм | + клипса цоколя | Кх2, Кх3, Кх4, Кх5, Кх1 | 22 |
| 19 | Комплект навески фасада ПММ | из поставки машины | Кх3 | 1 |
| 20 | Направляющие полного выдвижения с доводчиком NL 500 | пара | Кх4 | 3 |

## Примечания

1. Модели техники выбирает заказчик до изготовления мебели; ниши, вырезы и вентиляция — по монтажной схеме выбранной модели (условие гарантии), её номер вносится в ведомость.
2. Количество фурнитуры — по чертежам изделий; запас крепежа 5 %. Аналоги — по характеристикам (доводчик, нагрузка, ход).
3. Цвет корпусов, фасадов и профилей — по колерной карте проекта.

**Допущения и предложения на листе**

Основа листа: размеры сняты с растрового плана заказчика с частичными размерами: рисунок не в масштабе, помещения выровнены по подписанным размерам мебели и проходов; контрольный обмер не выполнен (К-1); высота потолка 2700 мм принята: на плане заказчика её нет (К-2); толщины стен 300 / 120 мм приняты по плану заказчика, не замерены (К-1); разрешённая мощность 15 кВт принята по типовым ТУ для квартиры, ТУ заказчиком не переданы (К-4).

См. лист открытых вопросов (лист 6, записи К-1, К-2, К-4).

| Изм. | Кол.уч | Лист | № док. | Подп. | Дата |
|---|---|---|---|---|---|
| Разраб. | | Кырлан А.С. | | | 18.10.26 |
| Пров. | | | | | |
| ГИП | | | | | |
| | | | | | |
| Н. контр. | | | | | |
| Утв. | | | | | |

**ГД-2026-008-АИ**

Квартира с кабинетом

Общая площадь 127,29* м² · * размеры со скана, не замерены (реестр — л. 6, К-1)

| Дизайн-проект интерьера | Стадия | Лист | Листов |
|---|---|---|---|
| | РП | 60 | 92 |

**Ведомости изделий, техники и фурнитуры**

М б/м

**Кырлан Александр Сергеевич**

выпуск 18.10.2026 № d2d5a25dca · стр. 70 из 129

09

# Развёртки и узлы

Кырлан Александр Сергеевич

выпуск 18.10.2026 · d2d5a25dca · стр. 71 из 129

# Реестр марок отделки и позиций альбома

Реестр марок отделки (О ↔ позиции колерной карты) и марки позиций по видам

ПРЕДВАРИТЕЛЬНО · не для производства работ · открыто пунктов: 4 (реестр — л. 6)

## Реестр марок отделки альбома

| Марка | Поверхность | Материал, изделие | Цвет, код | Помещения | Колер. карта |
|---|---|---|---|---|---|
| О1 | стены | окраска, Farrow & Ball Modern Emulsion, матовая, подготовка Q3 | Farrow & Ball No. 15 «Bone — мягкий каменно-серый с зеленцой» | 1, 3, 4, 5, 6, 8 | К1 |
| О2 | акцентная стена | окраска, Farrow & Ball Modern Emulsion, матовая, подготовка Q3 | Farrow & Ball No. 34 «Calke Green традиционный шалфей» | 1, 3, 4, 6 | К2 |
| О3 | плинтус | плинтус МДФ, h 80 мм, аналог: плинтус МДФ под покраску 80×16 | Farrow & Ball No. 15 «Bone — мягкий каменно-серый с зеленцой» | 1, 3, 4, 5, 8 | К4 |
| О4 | потолок | окраска, Tikkurila Anti-Reflex 2, глубокоматовая, подготовка Q3 | Tikkurila V503 «Winter» | 1, 2, 3, 4, 5, 6, 8 | К3 |
| О5 | пол | инженерная доска, Coswick Вековые традиции, 2100×127 мм, 1167-4250 |  | 1, 2, 3, 4, 5, 6 | КМ1 |
| О6 | стены | окраска, Tikkurila Harmony, матовая, подготовка Q3 | Tikkurila V503 «Winter» | 2 | К5 |
| О7 | плинтус | плинтус МДФ, h 80 мм, аналог: плинтус МДФ под покраску 80×16 | Tikkurila V503 «Winter» | 2 | К6 |
| О8 | фартук | керамогранит, 1200×600×9 мм, аналог: керамогранит под травертин, матовый, затирка CG2WA |  | 4 | КМ2 |
| О9 | плинтус | плинтус МДФ, Orac Decor Contour (Luxxus), h 69 мм, SX165 | Farrow & Ball No. 15 «Bone — мягкий каменно-серый с зеленцой» | 6 | К7 |
| О10 | стены | облицовка плиткой, Atlas Concorde Marvel Travertine, 600×1200×9 мм, A8UZ, затирка CG2WA | Atlas Concorde A8UZ «Marvel Travertine» | 7, 9 | К8 |
| О11 | потолок | окраска, Tikkurila Luja 7, матовая, подготовка Q3 | Tikkurila V503 «Winter» | 7, 9 | К9 |
| О12 | пол | керамогранит, Atlas Concorde Marvel Travertine, 600×1200×9 мм, A8UZ, затирка CG2WA | Atlas Concorde A8UZ «Marvel Travertine» | 7, 8, 9 | К8 |

## Марки позиций альбома по видам

| Префикс | Что обозначает, позиции | Листы |
|---|---|---|
| Д | двери: Д-1–Д-7 | 12–14 |
| ПР | проёмы без полотна (порталы): ПР-1, ПР-2 | 12–14 |
| ОК | окна: ОК-1–ОК-6 | 12–14 |
| Г, Д, К, Кх, П, С | мебель и оборудование: Г1, Г2, Д1, Д2, Д4, К1–К7, Кх1–Кх10, Кх12, Кх13, П8, П9, С1–С6 | 15–19 |
| П | сантехнические приборы: П1–П7, П10–П12 | 30–32 |
| ДК | декор (картины, зеркала, растения): ДК1–ДК9 | 1, 44–48 |
| Т | текстиль (шторы, ковры): Т1–Т25 | 1, 44–48 |
| S | выключатели: S1–S10, S11**, S12**, S13–S16 | 20–27 |
| Р | розетки: Р1–Р6, Р7**, Р8**, Р9–Р11, Р12**, Р13–Р16, Р17**, Р18**, Р19**, Р20–Р24, Р25**, Р29, Р32, Р33**, Р34 | 20–27 |

## Марки позиций альбома по видам (продолжение)

| Префикс | Что обозначает, позиции | Листы |
|---|---|---|
| LAN | розетки компьютерные: LAN1–LAN3 | 20–27 |
| Св | светильники: Св1–Св41, Св42**, Св43**, Св44**, Св45–Св48, Св49**, Св50–Св54 | 20–27 |
| БП | блоки питания LED: БП1–БП4, БП5** | 20–27 |
| ИП | извещатели: ИП1–ИП6 | 20–27 |
| ТВ | розетки ТВ: ТВ1, ТВ2 | 20–27 |
| ЭВ | выводы кабеля: ЭВ1–ЭВ3, ЭВ4**, ЭВ5**, ЭВ6**, ЭВ7** | 20–27 |
| АР | точки доступа Wi-Fi: АР1**, АР2** | 20–27 |
| КУП | электроустановочные изделия: КУП1**, КУП2** | 20–27 |
| ЩК, ЩС** | щиты: ЩК, ЩС** | 20–27 |
| ДФ | домофон: ДФ1 | 20–27 |
| Ст В1, Ст К1, Ст К1-3 (кухня), Ст Т3 | стояки (системы В1, Т3, К1): Ст В1-1, Ст В1-2, Ст В1-3, Ст К1-1, Ст К1-2, Ст К1-3 (кухня), Ст Т3-1, Ст Т3-2, Ст Т3-3 | 30–32 |
| О | марки отделки (реестр альбома): О1–О12 | 2–5, 61–85 |
| К, КМ | позиции колерной карты: К1–К9, КМ1, КМ2 | 42, 43 |
| РО | радиаторы отопления: РО-1–РО-9 | 28, 29 |

## Примечания

1. Марка отделки О — одна на весь альбом: одна и та же отделка (материал, изделие, цвет, формат) на всех листах имеет одну марку; на развёртках и планах стоят марки этого реестра.
2. Столбец «Колер. карта» — позиции колерной карты (лист 42): К — окраска по коду цвета, КМ — материал без кода цвета; «Помещения» — номера по экспликации; количества — по ведомости отделки помещений (лист 40).
3. Марки позиций: один префикс — один вид позиций на весь альбом (двери Д, окна ОК, мебель М, сантехприборы П, декор ДК, текстиль Т, колерная карта К и КМ, радиаторы РО, розетки Р, выключатели S, светильники Св; стояки — «Ст» и система, например «Ст К1-1»). Совпадение префиксов у разных видов — замечание к исходным данным, при выпуске исправляется в модели.

Допущения и предложения на листе. Основа листа: размеры сняты с растрового плана заказчика с частичными размерами: рисунок не в масштабе, помещения выровнены по подписанным размерам мебели и проходов; контрольный обмер не выполнен (К-1); высота потолка 2700 мм принята: на плане заказчика её нет (К-2); толщины стен 300 / 120 мм приняты по плану заказчика, не замерены (К-1); разрешённая мощность 15 кВт принята по типовым ТУ для квартиры, ТУ заказчиком не переданы (К-4). Знак «**» — предложено, не утверждено (согласовать): записи в реестре нет: плинтус пом. 1–5, 8, фартук пом. 4, Р12, S11, S12, Р18, Р19, Р25, Св42, Св43, Св44, Св49, БП5, Р7, Р8, ЭВ4, КУП1, ЭВ6, Р17, Р33, ЭВ5, КУП2, ЭВ7, АР2, ЩС, АР1. См. лист открытых вопросов (лист 6, записи К-1, К-2, К-4).

| Изм. | Кол.уч | Лист | № док. | Подп. | Дата |
|---|---|---|---|---|---|
| Разраб. |  | Кырлан А.С. |  |  | 18.10.26 |
| Пров. |  |  |  |  |  |
| ГИП |  |  |  |  |  |
|  |  |  |  |  |  |
| Н. контр. |  |  |  |  |  |
| Утв. |  |  |  |  |  |

**ГД-2026-008-АИ**

Квартира с кабинетом

Общая площадь 127,29* м² · * размеры со скана, не замерены (реестр — л. 6, К-1)

Дизайн-проект интерьера

| Стадия | Лист | Листов |
|---|---|---|
| РП | 61 | 92 |

**Реестр марок отделки и позиций альбома**

М б/м

**Кырлан Александр Сергеевич**

выпуск 18.10.2026 № d2d5a25dca · стр. 72 из 129

# Схема расположения развёрток и узлов

План квартиры: марки развёрток по помещениям, выноски узлов, ведомость «марка → лист»

**ПРЕДВАРИТЕЛЬНО · не для производства работ · открыто пунктов: 4 (реестр — л. 6)**

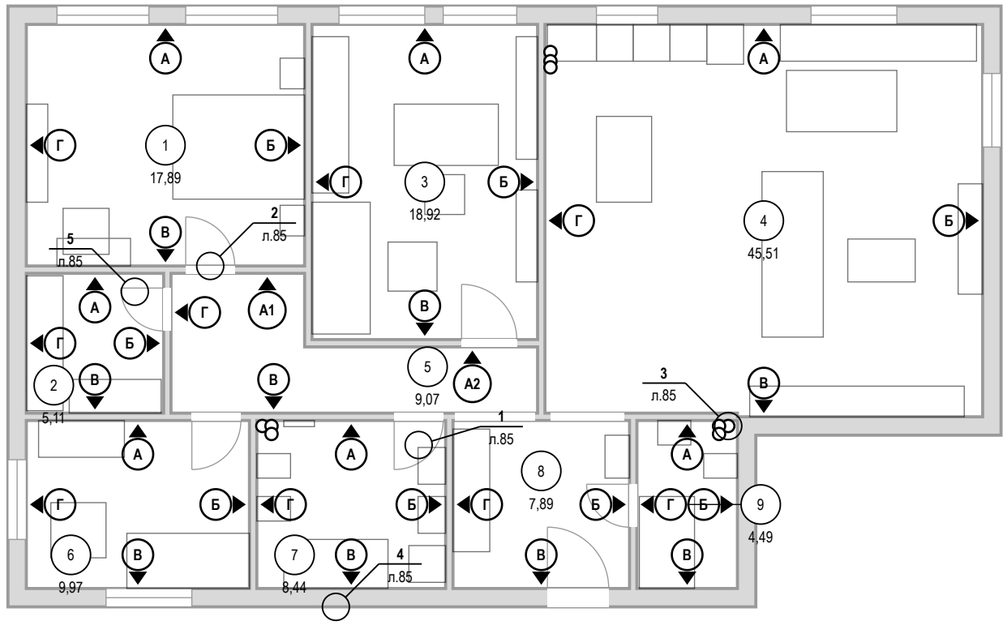


## Развёртки и узлы: марка → лист

| Марка | Помещение / узел | Лист |
|---|---|---|
| А, Б | Спальня (пом. 1) | 63 |
| В, Г | Спальня (пом. 1) | 64 |
| А, Б, В | Гардеробная-постирочная (пом. 2) | 65 |
| Г | Гардеробная-постирочная (пом. 2) | 66 |
| А, Б | Кабинет (пом. 3) | 67 |
| В, Г | Кабинет (пом. 3) | 68 |
| Г | Кухня-гостиная (пом. 4) | 69 |
| А | Кухня-гостиная (пом. 4) | 70 |
| Б | Кухня-гостиная (пом. 4) | 71 |
| В | Кухня-гостиная (пом. 4) | 72 |
| А1, А2 | Коридор (пом. 5) | 73 |
| В, Г | Коридор (пом. 5) | 74 |
| А, Б | Детская (пом. 6) | 75 |
| В, Г | Детская (пом. 6) | 76 |
| А | Ванная (пом. 7) | 77 |
| Б | Ванная (пом. 7) | 78 |
| В | Ванная (пом. 7) | 79 |
| Г | Ванная (пом. 7) | 80 |
| Б, В, Г | Прихожая (пом. 8) | 81 |
| А | Санузел гостевой (пом. 9) | 82 |
| Б, В | Санузел гостевой (пом. 9) | 83 |
| Г | Санузел гостевой (пом. 9) | 84 |
| узел 1 | Порог 15 мм: мокрая зона — жилое помещение | 85 |
| узел 2 | Дверь скрытого монтажа в плоскости стены, плинтус | 85 |
| узел 3 | Короб стояков К1-1 с люком и звукоизоляцией | 85 |
| узел 4 | Гидроизоляция санузла: заход на стены 200 мм, примыкание ванны | 85 |
| узел 5 | Плинтус МДФ 80×16 мм у окрашенной стены | 85 |

**Допущения и предложения на листе**

Основа листа: размеры сняты с растрового плана заказчика с частичными размерами: рисунок не в масштабе, помещения выровнены по подписанным размерам мебели и проходов; контрольный обмер не выполнен (К-1); высота потолка 2700 мм принята: на плане заказчика её нет (К-2); толщины стен 300 / 120 мм приняты по плану заказчика, не замерены (К-1); разрешённая мощность 15 кВт принята по типовым ТУ для квартиры, ТУ заказчиком не переданы (К-4).

См. лист открытых вопросов (лист 6, записи К-1, К-2, К-4).

### Условные обозначения

- (А) — марка развёртки: буква стены, стрелка — взгляд
- выноска узла: над полкой — узел, под полкой — лист
- (1) — номер помещения, площадь м²

1000 мм · печать 1:1

### Примечания

1. Развёртки — вид на стену изнутри помещения; буквы стен — одна система на весь альбом (как на листах выводов, плитки и отделки).
2. Стены без электроточек, мебели, декора и акцентной отделки развёрток не имеют: их отделка — по ведомости отделки помещений.
3. Узлы — на листе узлов; места применения — по выноскам этого листа и ведомости «марка → лист».

| Изм. | Кол.уч | Лист | № док. | Подп. | Дата |
|---|---|---|---|---|---|
| Разраб. | | Кырлан А.С. | | | 18.10.26 |
| Пров. | | | | | |
| ГИП | | | | | |
| | | | | | |
| Н. контр. | | | | | |
| Утв. | | | | | |

**ГД-2026-008-АИ**

Квартира с кабинетом

Общая площадь 127,29* м² · * размеры со скана, не замерены (реестр — л. 6, К-1)

Дизайн-проект интерьера

| Стадия | Лист | Листов |
|---|---|---|
| РП | 62 | 92 |

**Схема расположения развёрток и узлов**

М 1:100

**Кырлан Александр Сергеевич**

выпуск 18.10.2026 № d2d5a25dca · стр. 73 из 129

# Развёртки стен А, Б. Спальня (пом. 1)

Спальня (пом. 1) · вид изнутри помещения · размеры в мм, отметки в м

ПРЕДВАРИТЕЛЬНО · не для производства работ · открыто пунктов: 4 (реестр — л. 6)

## Развёртка стены А

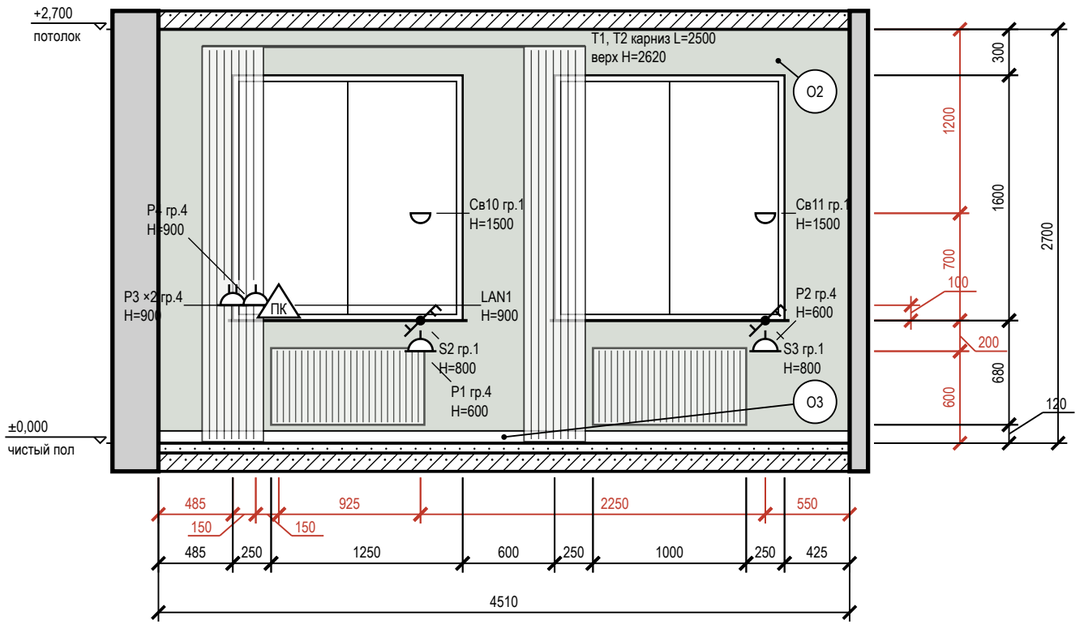


## Развёртка стены Б

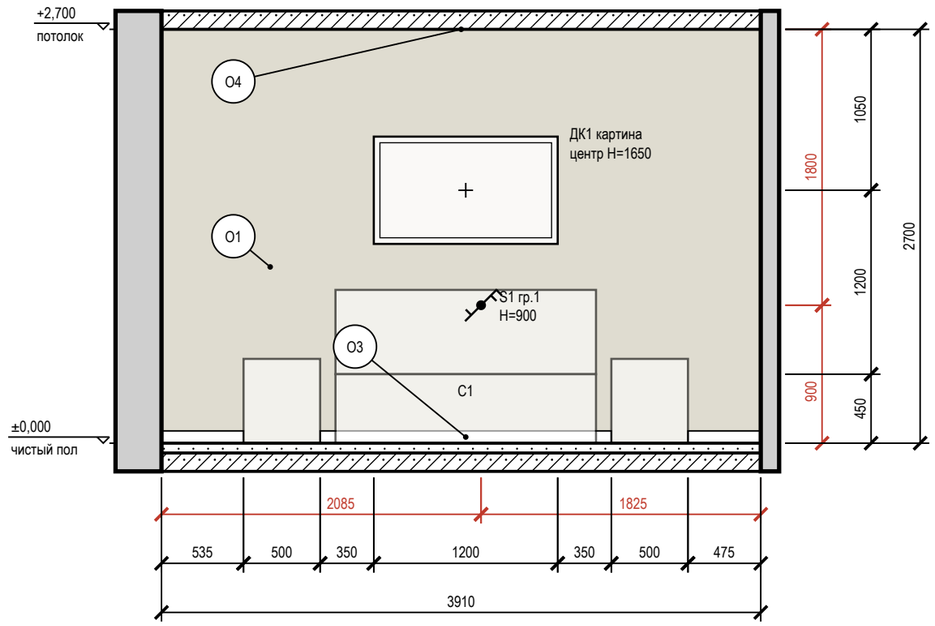


## Схема развёрток (М 1:100)

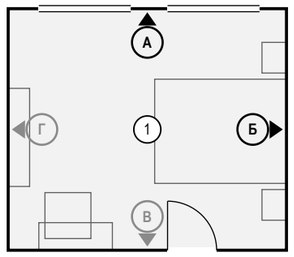


## Условные обозначения

- розетка с заземляющим контактом; у знака — марка, ×N постов в рамке, гр. — группа щита, H — высота оси, мм
- выключатель одноклавишный
- выключатель двухклавишный (флажков — по числу клавиш)
- выключатель с проходной или перекрёстной клавишей (обратный флажок); тип клавиши — в подписи
- светильник настенный (бра), H — высота оси
- розетка компьютерная RJ45
- привязки точек и выводов от угла и от пола, мм
- мебель и приборы — фасад по расстановке (условно)
- картина (декор): марка Д, крест — центр, H — высота центра, мм
- карниз (шина) и шторы в собранном виде: марка T, длина L, верх H
- окно: проём, рама, подоконник
- радиатор отопления; марка — по плану отопления
- стены и перекрытия в сечении
- окраска: тон — цвет по коду производителя (условно)
- O1 — марка отделки по реестру отделки альбома
- А — марка развёртки: буква стены, стрелка — взгляд

## Ведомость отделки (на листе)

| Марка | Поверхность | Материал, изделие | Цвет, код | Кол. |
|---|---|---|---|---|
| O1 | стены | окраска, Farrow & Ball Modern Emulsion, матовая, подготовка Q3 | Farrow & Ball No. 15 «Bone — мягкий каменно-серый с зеленцой» | 10,6 м² |
| O2 | акцентная стена | окраска, Farrow & Ball Modern Emulsion, матовая, подготовка Q3 | Farrow & Ball No. 34 «Calke Green традиционный шалфей» | 7,4 м² |
| O3 | плинтус | плинтус МДФ, h 80 мм, аналог: плинтус МДФ под покраску 80×16 | Farrow & Ball No. 15 «Bone — мягкий каменно-серый с зеленцой» | 7,4 м |
| O4 | потолок | окраска, Tikkurila Anti-Reflex 2, глубокоматовая, подготовка Q3 | Tikkurila V503 «Winter» | 17,9 м² |

**Допущения и предложения на листе**

Основа листа: размеры сняты с растрового плана заказчика с частичными размерами: рисунок не в масштабе, помещения выровнены по подписанным размерам мебели и проходов; контрольный обмер не выполнен (К-1); высота потолка 2700 мм принята: на плане заказчика её нет (К-2); толщины стен 300 / 120 мм приняты по плану заказчика, не замерены (К-1); разрешённая мощность 15 кВт принята по типовым ТУ для квартиры, ТУ заказчиком не переданы (К-4).
См. лист открытых вопросов (лист 6, записи К-1, К-2, К-4).

## Примечания

1. Развёртки — вид на стену изнутри помещения, по часовой стрелке; расположение — на схеме листа и на листе 62; размеры — в мм по чистовым поверхностям; отметки — в м от ±0,000; высоты H — от чистого пола помещения до оси изделия, у декора — до центра.
2. Красные цепочки — привязки электроточек и выводов: по горизонтали от угла чистовых стен, по вертикали от чистого пола, до оси изделия; звенья короче 3 мм на листе вынесены во второй ярус (ближняя к стене цепочка).
3. У знака электроточки: марка (Р — розетка, S — выключатель, Св — светильник, ЭВ — вывод кабеля), ×N — число постов в рамке, гр. — группа щита, H — высота оси от чистого пола, мм; группы по клавишам выключателя — на листе выключателей.
4. Схема мебели, приборов и декора не является технической документацией для производства мебели; габариты — по паспортам изделий.
5. Картины и зеркала крепить к основанию по паспорту изделия (закладные и анкеры — в перечне скрытых работ); крест — ось центра предмета.
6. Карнизы (шины) — по ведомости текстиля декоратора; длина L и верх H — по развёртке, крепление — до окраски потолка.
7. Линии узора (швы плитки, складки штор, рёбра радиаторов) прерываются у знаков и выносок — просвет между линиями не менее 0,7 мм.

1000 мм · печать 1:1

| Изм. | Кол.уч | Лист | № док. | Подп. | Дата |
|---|---|---|---|---|---|
| Разраб. | | Кырлан А.С. | | | 18.10.26 |
| Пров. | | | | | |
| ГИП | | | | | |
| | | | | | |
| Н. контр. | | | | | |
| Утв. | | | | | |

**ГД-2026-008-АИ**

Квартира с кабинетом

Общая площадь 127,29* м² · * размеры со скана, не замерены (реестр — л. 6, К-1)

Дизайн-проект интерьера

| Стадия | Лист | Листов |
|---|---|---|
| РП | 63 | 92 |

**Развёртки стен А, Б. Спальня (пом. 1)**

М 1:40

**Кырлан Александр Сергеевич**

выпуск 18.10.2026 № d2d5a25dca · стр. 74 из 129

# Развёртки стен В, Г. Спальня (пом. 1)

Спальня (пом. 1) · вид изнутри помещения · размеры в мм, отметки в м

ПРЕДВАРИТЕЛЬНО · не для производства работ · открыто пунктов: 4 (реестр — л. 6)

**Развёртка стены В**

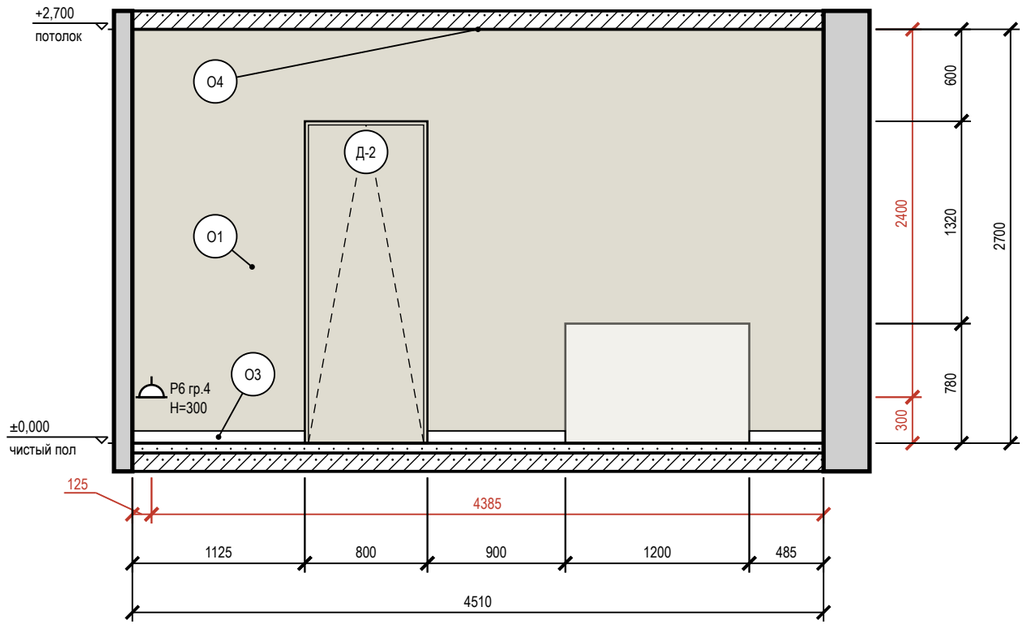


**Развёртка стены Г**

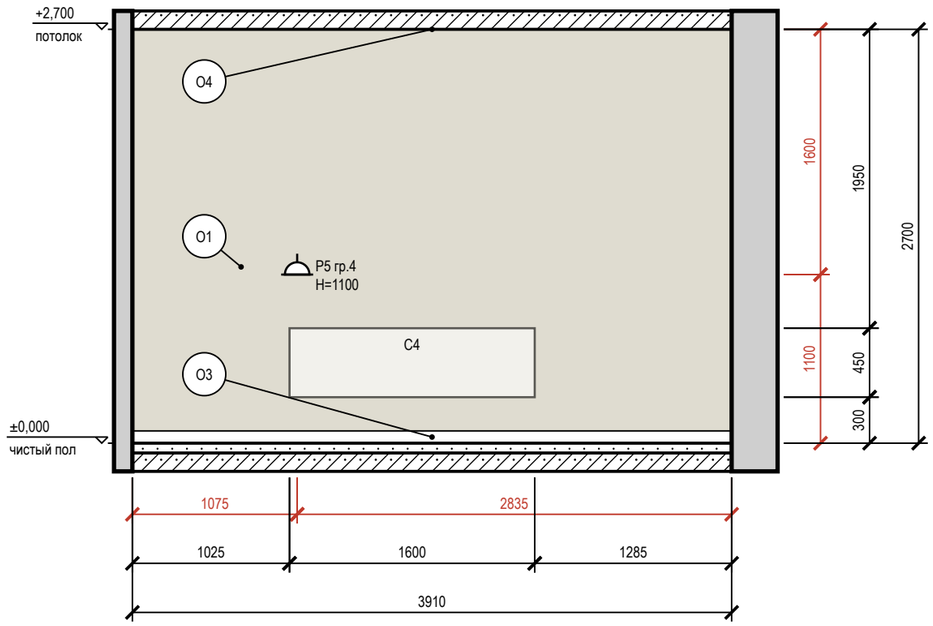


## Схема развёрток (М 1:100)

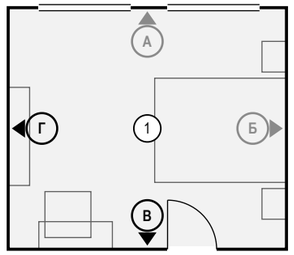


## Условные обозначения

- розетка с заземляющим контактом; у знака — марка, ×N постов в рамке, гр. — группа щита, H — высота оси, мм
- привязки точек и выводов от угла и от пола, мм
- мебель и приборы — фасад по расстановке (условно)
- дверь скрытого монтажа: полотно в плоскости стены (узел — на листе узлов)
- стены и перекрытия в сечении
- окраска: тон — цвет по коду производителя (условно)
- О1 — марка отделки по реестру отделки альбома
- А — марка развёртки: буква стены, стрелка — взгляд

## Ведомость отделки (на листе)

| Марка | Поверхность | Материал, изделие | Цвет, код | Кол. |
|---|---|---|---|---|
| О1 | стены | окраска, Farrow & Ball Modern Emulsion, матовая, подготовка Q3 | Farrow & Ball No. 15 «Bone — мягкий каменно-серый с зеленцой» | 21,1 м² |
| О3 | плинтус | плинтус МДФ, h 80 мм, аналог: плинтус МДФ под покраску 80×16 | Farrow & Ball No. 15 «Bone — мягкий каменно-серый с зеленцой» | 6,4 м |
| О4 | потолок | окраска, Tikkurila Anti-Reflex 2, глубокоматовая, подготовка Q3 | Tikkurila V503 «Winter» | 17,9 м² |

**Допущения и предложения на листе**

Основа листа: размеры сняты с растрового плана заказчика с частичными размерами: рисунок не в масштабе, помещения выровнены по подписанным размерам мебели и проходов; контрольный обмер не выполнен (К-1); высота потолка 2700 мм принята: на плане заказчика её нет (К-2); толщины стен 300 / 120 мм приняты по плану заказчика, не замерены (К-1); разрешённая мощность 15 кВт принята по типовым ТУ для квартиры, ТУ заказчиком не переданы (К-4).
См. лист открытых вопросов (лист 6, записи К-1, К-2, К-4).

## Примечания

1. Развёртки — вид на стену изнутри помещения, по часовой стрелке; расположение — на схеме листа и на листе 62; размеры — в мм по чистовым поверхностям; отметки — в м от ±0,000; высоты H — от чистого пола помещения до оси изделия, у декора — до центра.
2. Красные цепочки — привязки электроточек и выводов: по горизонтали от угла чистовых стен, по вертикали от чистого пола, до оси изделия; звенья короче 3 мм на листе вынесены во второй ярус (ближняя к стене цепочка).
3. У знака электроточки: марка (Р — розетка, S — выключатель, Св — светильник, ЭВ — вывод кабеля), ×N — число постов в рамке, гр. — группа щита, H — высота оси от чистого пола, мм; группы по клавишам выключателя — на листе выключателей.
4. Схема мебели, приборов и декора не является технической документацией для производства мебели; габариты — по паспортам изделий.
5. Двери скрытого монтажа — полотно в плоскости стены, отделка стены по полотну, плинтус прерывается у короба (узел — на листе узлов).

1000 мм · печать 1:1

| Изм. | Кол.уч | Лист | № док. | Подп. | Дата |
|---|---|---|---|---|---|
| Разраб. | | Кырлан А.С. | | | 18.10.26 |
| Пров. | | | | | |
| ГИП | | | | | |
| | | | | | |
| Н. контр. | | | | | |
| Утв. | | | | | |

**ГД-2026-008-АИ**

Квартира с кабинетом

Общая площадь 127,29* м² · * размеры со скана, не замерены (реестр — л. 6, К-1)

| Дизайн-проект интерьера | Стадия | Лист | Листов |
|---|---|---|---|
| | РП | 64 | 92 |
| **Развёртки стен В, Г. Спальня (пом. 1)** М 1:40 | **Кырлан Александр Сергеевич** | | |

выпуск 18.10.2026 № d2d5a25dca · стр. 75 из 129

# Развёртки стен А, Б, В. Гардеробная-постирочная (пом. 2)

Гардеробная-постирочная (пом. 2) · вид изнутри помещения · размеры в мм, отметки в м

**ПРЕДВАРИТЕЛЬНО · не для производства работ · открыто пунктов: 4 (реестр — л. 6)**

### Развёртка стены А

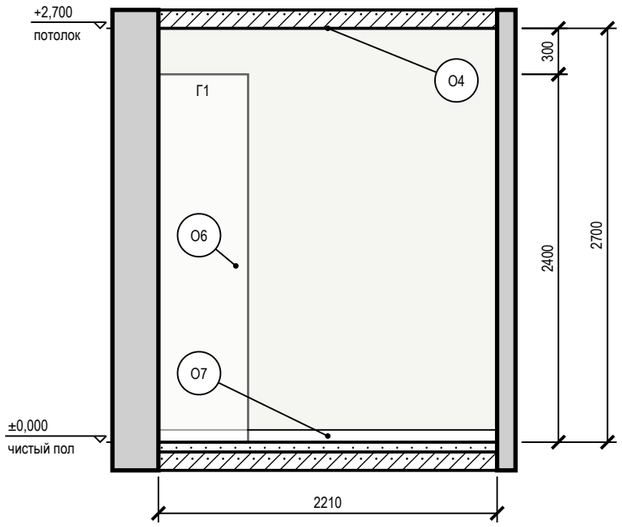


### Развёртка стены Б

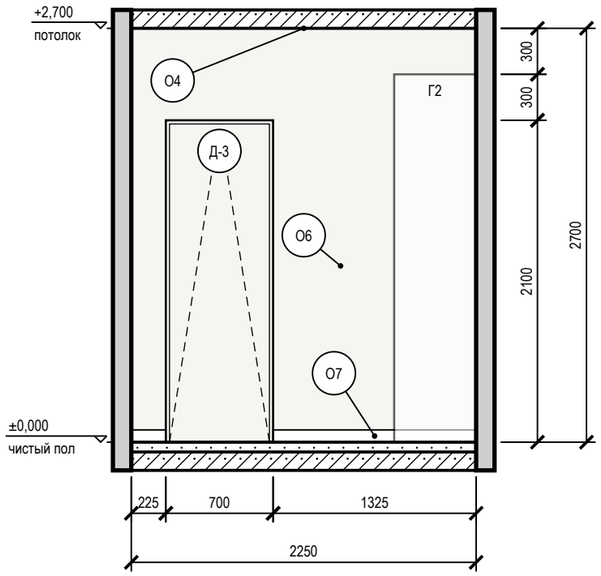


### Развёртка стены В

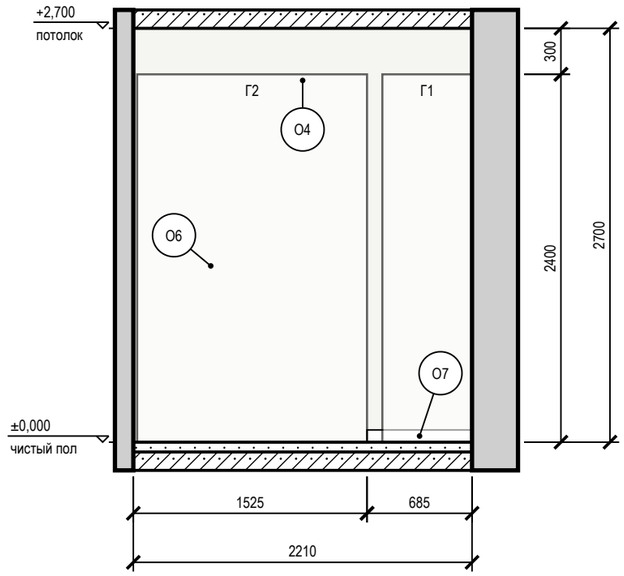


### Схема развёрток (М 1:100)

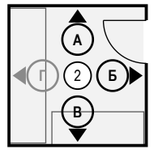


## Условные обозначения

- привязки точек и выводов от угла и от пола, мм
- мебель и приборы — фасад по расстановке (условно)
- дверь скрытого монтажа: полотно в плоскости стены (узел — на листе узлов)
- стены и перекрытия в сечении
- окраска: тон — цвет по коду производителя (условно)
- О1 — марка отделки по реестру отделки альбома
- А — марка развёртки: буква стены, стрелка — взгляд

## Ведомость отделки (на листе)

| Марка | Поверхность | Материал, изделие | Цвет, код | Кол. |
|---|---|---|---|---|
| О4 | потолок | окраска, Tikkurila Anti-Reflex 2, глубокоматовая, подготовка Q3 | Tikkurila V503 «Winter» | 5,1 м² |
| О6 | стены | окраска, Tikkurila Harmony, матовая, подготовка Q3 | Tikkurila V503 «Winter» | 16,5 м² |
| О7 | плинтус | плинтус МДФ, h 80 мм, аналог: плинтус МДФ под покраску 80×16 | Tikkurila V503 «Winter» | 4,4 м |

**Допущения и предложения на листе**

Основа листа: размеры сняты с растрового плана заказчика с частичными размерами: рисунок не в масштабе, помещения выровнены по подписанным размерам мебели и проходов; контрольный обмер не выполнен (К-1); высота потолка 2700 мм принята: на плане заказчика её нет (К-2); толщины стен 300 / 120 мм приняты по плану заказчика, не замерены (К-1); разрешённая мощность 15 кВт принята по типовым ТУ для квартиры, ТУ заказчиком не переданы (К-4).

См. лист открытых вопросов (лист 6, записи К-1, К-2, К-4).

## Примечания

1. Развёртки — вид на стену изнутри помещения, по часовой стрелке; расположение — на схеме листа и на листе 62; размеры — в мм по чистовым поверхностям; отметки — в м от ±0,000; высоты Н — от чистого пола помещения до оси изделия, у декора — до центра.
2. Красные цепочки — привязки электроточек и выводов: по горизонтали от угла чистовых стен, по вертикали от чистого пола, до оси изделия; звенья короче 3 мм на листе вынесены во второй ярус (ближняя к стене цепочка).
3. У знака электроточки: марка (Р — розетка, S — выключатель, Св — светильник, ЭВ — вывод кабеля), ×N — число постов в рамке, гр. — группа щита, Н — высота оси от чистого пола, мм; группы по клавишам выключателя — на листе выключателей.
4. Схема мебели, приборов и декора не является технической документацией для производства мебели; габариты — по паспортам изделий.
5. Двери скрытого монтажа — полотно в плоскости стены, отделка стены по полотну, плинтус прерывается у короба (узел — на листе узлов).

1000 мм · печать 1:1

| Изм. | Кол.уч | Лист | № док. | Подп. | Дата |
|---|---|---|---|---|---|
| Разраб. | | Кырлан А.С. | | | 18.10.26 |
| Пров. | | | | | |
| ГИП | | | | | |
| | | | | | |
| Н. контр. | | | | | |
| Утв. | | | | | |

**ГД-2026-008-АИ**

Квартира с кабинетом

Общая площадь 127,29* м² · * размеры со скана, не замерены (реестр — л. 6, К-1)

Дизайн-проект интерьера

| Стадия | Лист | Листов |
|---|---|---|
| РП | 65 | 92 |

**Развёртки стен А, Б, В.**
**Гардеробная-постирочная (пом. 2)**
М 1:40

**Кырлан Александр Сергеевич**

выпуск 18.10.2026 · d2d5a25dca · стр. 76 из 129

# Развёртка стены Г. Гардеробная-постирочная (пом. 2)

Гардеробная-постирочная (пом. 2) · вид изнутри помещения · размеры в мм, отметки в м

**ПРЕДВАРИТЕЛЬНО · не для производства работ · открыто пунктов: 4 (реестр — л. 6)**

## Развёртка стены Г

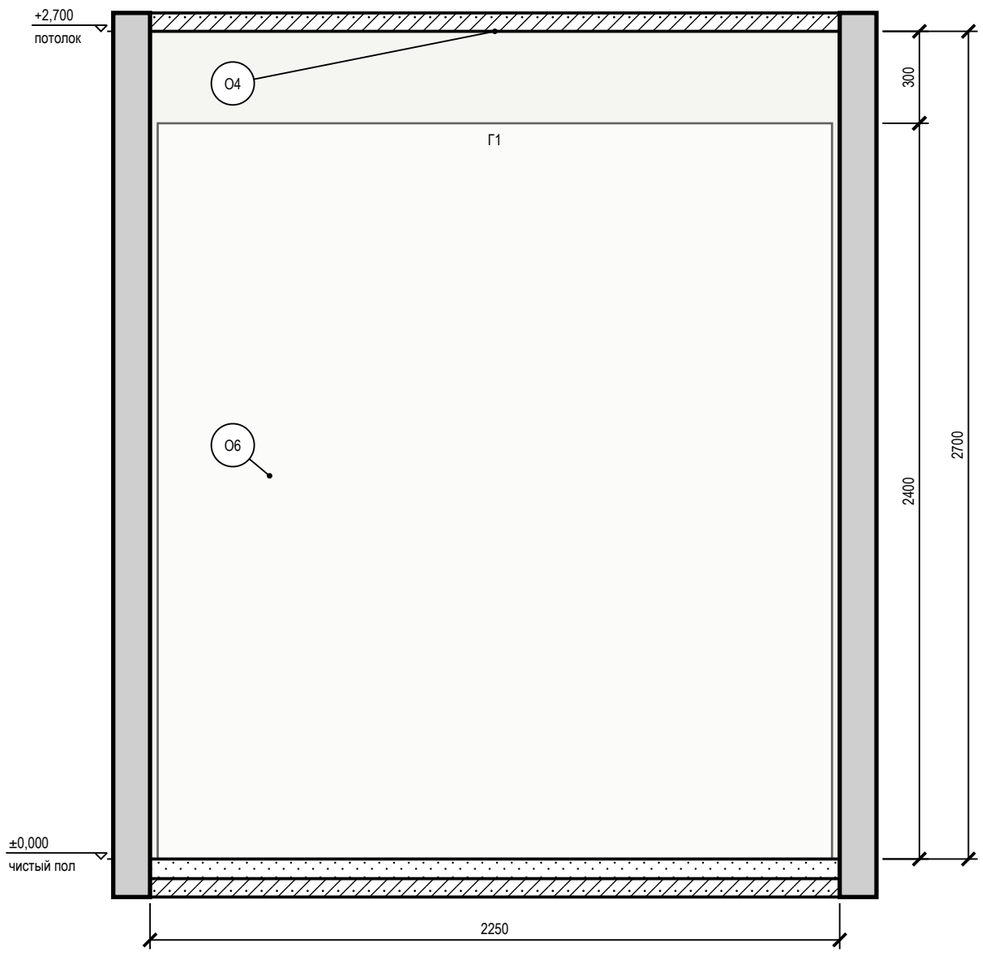


## Схема развёрток (М 1:100)

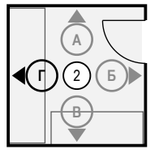


## Условные обозначения

- привязки точек и выводов от угла и от пола, мм
- мебель и приборы — фасад по расстановке (условно)
- стены и перекрытия в сечении
- окраска: тон — цвет по коду производителя (условно)
- О1 — марка отделки по реестру отделки альбома
- А — марка развёртки: буква стены, стрелка — взгляд

## Ведомость отделки (на листе)

| Марка | Поверхность | Материал, изделие | Цвет, код | Кол. |
|---|---|---|---|---|
| О4 | потолок | окраска, Tikkurila Anti-Reflex 2, глубокоматовая, подготовка Q3 | Tikkurila V503 «Winter» | 5,1 м² |
| О6 | стены | окраска, Tikkurila Harmony, матовая, подготовка Q3 | Tikkurila V503 «Winter» | 6,1 м² |

**Допущения и предложения на листе**

Основа листа: размеры сняты с растрового плана заказчика с частичными размерами: рисунок не в масштабе, помещения выровнены по подписанным размерам мебели и проходов; контрольный обмер не выполнен (К-1); высота потолка 2700 мм принята: на плане заказчика её нет (К-2); толщины стен 300 / 120 мм приняты по плану заказчика, не замерены (К-1); разрешённая мощность 15 кВт принята по типовым ТУ для квартиры, ТУ заказчиком не переданы (К-4).

См. лист открытых вопросов (лист 6, записи К-1, К-2, К-4).

## Примечания

1. Развёртки — вид на стену изнутри помещения, по часовой стрелке; расположение — на схеме листа и на листе 62; размеры — в мм по чистовым поверхностям; отметки — в м от ±0,000; высоты Н — от чистого пола помещения до оси изделия, у декора — до центра.
2. Красные цепочки — привязки электроточек и выводов: по горизонтали от угла чистовых стен, по вертикали от чистого пола, до оси изделия; звенья короче 3 мм на листе вынесены во второй ярус (ближняя к стене цепочка).
3. У знака электроточки: марка (Р — розетка, S — выключатель, Св — светильник, ЭВ — вывод кабеля), ×N — число постов в рамке, гр. — группа щита, Н — высота оси от чистого пола, мм; группы по клавишам выключателя — на листе выключателей.
4. Схема мебели, приборов и декора не является технической документацией для производства мебели; габариты — по паспортам изделий.

1000 мм · печать 1:1

| Изм. | Кол.уч | Лист | № док. | Подп. | Дата |
|---|---|---|---|---|---|
| Разраб. | | Кырлан А.С. | | | 18.10.26 |
| Пров. | | | | | |
| ГИП | | | | | |
| | | | | | |
| Н. контр. | | | | | |
| Утв. | | | | | |

**ГД-2026-008-АИ**

Квартира с кабинетом

Общая площадь 127,29* м² · * размеры со скана, не замерены (реестр — л. 6, К-1)

Дизайн-проект интерьера

| Стадия | Лист | Листов |
|---|---|---|
| РП | 66 | 92 |

**Развёртка стены Г. Гардеробная-постирочная (пом. 2)**

М 1:20

**Кырлан Александр Сергеевич**

выпуск 18.10.2026 · d2d5a25dca · стр. 77 из 129

# Развёртки стен А, Б. Кабинет (пом. 3)

Кабинет (пом. 3) · вид изнутри помещения · размеры в мм, отметки в м

ПРЕДВАРИТЕЛЬНО · не для производства работ · открыто пунктов: 4 (реестр — л. 6)

## Развёртка стены А

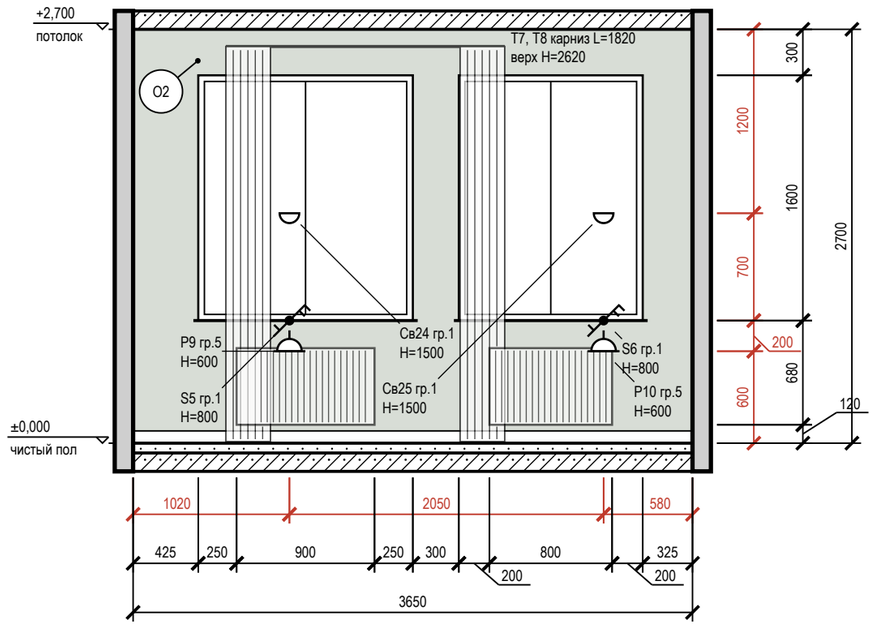


## Развёртка стены Б

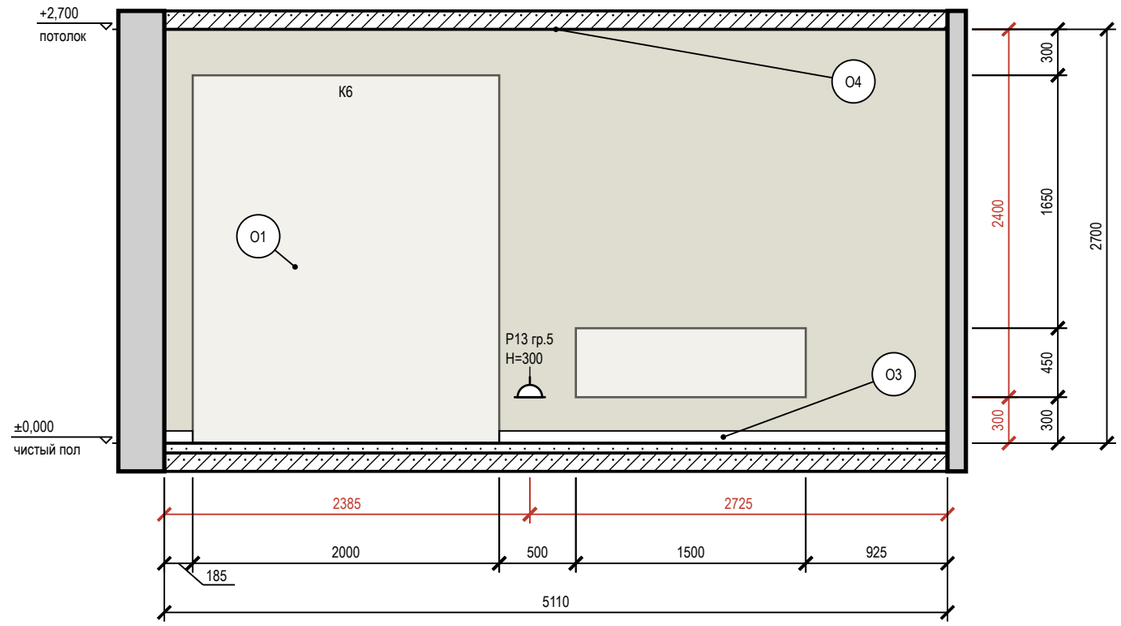


## Схема развёрток (М 1:100)

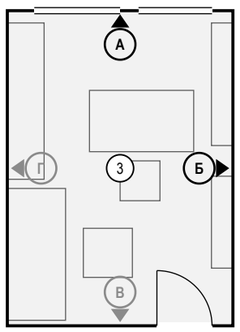


## Условные обозначения

- розетка с заземляющим контактом; у знака — марка, ×N постов в рамке, гр. — группа щита, Н — высота оси, мм
- выключатель одноклавишный
- выключатель двухклавишный (флажков — по числу клавиш)
- выключатель с проходной или перекрёстной клавишей (обратный флажок); тип клавиши — в подписи
- светильник настенный (бра), Н — высота оси
- привязки точек и выводов от угла и от пола, мм
- мебель и приборы — фасад по расстановке (условно)
- карниз (шина) и шторы в собранном виде: марка Т, длина L, верх Н
- окно: проём, рама, подоконник
- радиатор отопления; марка — по плану отопления
- стены и перекрытия в сечении
- окраска: тон — цвет по коду производителя (условно)
- О1 — марка отделки по реестру отделки альбома
- А — марка развёртки: буква стены, стрелка — взгляд

## Ведомость отделки (на листе)

| Марка | Поверхность | Материал, изделие | Цвет, код | Кол. |
|---|---|---|---|---|
| О1 | стены | окраска, Farrow & Ball Modern Emulsion, матовая, подготовка Q3 | Farrow & Ball No. 15 «Bone — мягкий каменно-серый с зеленцой» | 13,8 м² |
| О2 | акцентная стена | окраска, Farrow & Ball Modern Emulsion, матовая, подготовка Q3 | Farrow & Ball No. 34 «Calke Green традиционный шалфей» | 5,7 м² |
| О3 | плинтус | плинтус МДФ, h 80 мм, аналог: плинтус МДФ под покраску 80×16 | Farrow & Ball No. 15 «Bone — мягкий каменно-серый с зеленцой» | 6,8 м |
| О4 | потолок | окраска, Tikkurila Anti-Reflex 2, глубокоматовая, подготовка Q3 | Tikkurila V503 «Winter» | 18,9 м² |

**Допущения и предложения на листе**

Основа листа: размеры сняты с растрового плана заказчика с частичными размерами: рисунок не в масштабе, помещения выровнены по подписанным размерам мебели и проходов; контрольный обмер не выполнен (К-1); высота потолка 2700 мм принята: на плане заказчика её нет (К-2); толщины стен 300 / 120 мм приняты по плану заказчика, не замерены (К-1); разрешённая мощность 15 кВт принята по типовым ТУ для квартиры, ТУ заказчиком не переданы (К-4).
См. лист открытых вопросов (лист 6, записи К-1, К-2, К-4).

## Примечания

1. Развёртки — вид на стену изнутри помещения, по часовой стрелке; расположение — на схеме листа и на листе 62; размеры — в мм по чистовым поверхностям; отметки — в м от ±0,000; высоты Н — от чистого пола помещения до оси изделия, у декора — до центра.
2. Красные цепочки — привязки электроточек и выводов: по горизонтали от угла чистовых стен, по вертикали от чистого пола, до оси изделия; звенья короче 3 мм на листе вынесены во второй ярус (ближняя к стене цепочка).
3. У знака электроточки: марка (Р — розетка, S — выключатель, Св — светильник, ЭВ — вывод кабеля), ×N — число постов в рамке, гр. — группа щита, Н — высота оси от чистого пола, мм; группы по клавишам выключателя — на листе выключателей.
4. Схема мебели, приборов и декора не является технической документацией для производства мебели; габариты — по паспортам изделий.
5. Карнизы (шины) — по ведомости текстиля декоратора; длина L и верх Н — по развёртке, крепление — до окраски потолка.
6. Линии узора (швы плитки, складки штор, рёбра радиаторов) прерываются у знаков и выносок — просвет между линиями не менее 0,7 мм.

1000 мм · печать 1:1

| Изм. | Кол.уч | Лист | № док. | Подп. | Дата |
|---|---|---|---|---|---|
| Разраб. | | Кырлан А.С. | | | 18.10.26 |
| Пров. | | | | | |
| ГИП | | | | | |
| | | | | | |
| Н. контр. | | | | | |
| Утв. | | | | | |

**ГД-2026-008-АИ**

Квартира с кабинетом

Общая площадь 127,29* м² · * размеры со скана, не замерены (реестр — л. 6, К-1)

Дизайн-проект интерьера

| Стадия | Лист | Листов |
|---|---|---|
| РП | 67 | 92 |

**Развёртки стен А, Б. Кабинет (пом. 3)**

М 1:40

**Кырлан Александр Сергеевич**

выпуск 18.10.2026 · d2d5a25dca · стр. 78 из 129

# Развёртки стен В, Г. Кабинет (пом. 3)

Кабинет (пом. 3) · вид изнутри помещения · размеры в мм, отметки в м

ПРЕДВАРИТЕЛЬНО · не для производства работ · открыто пунктов: 4 (реестр — л. 6)

## Развёртка стены В

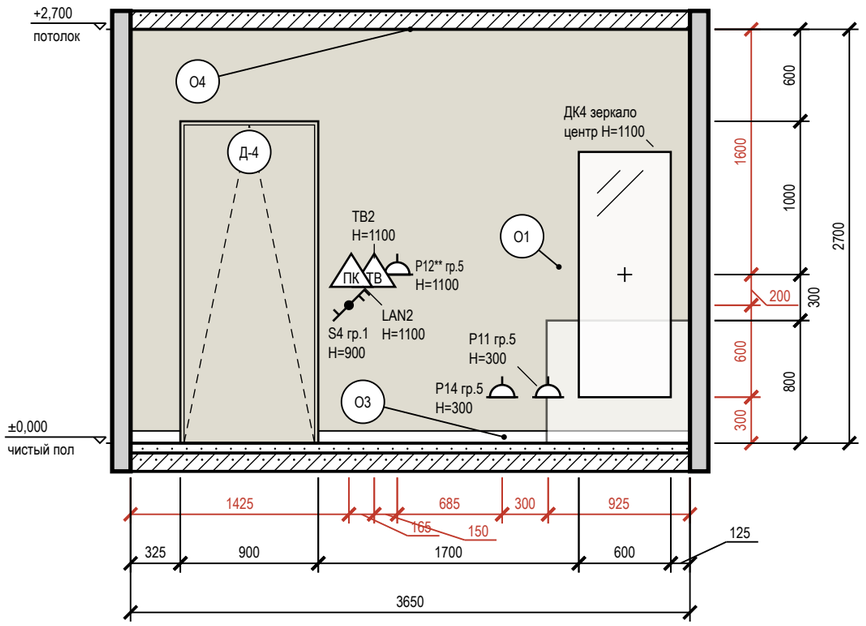


## Развёртка стены Г

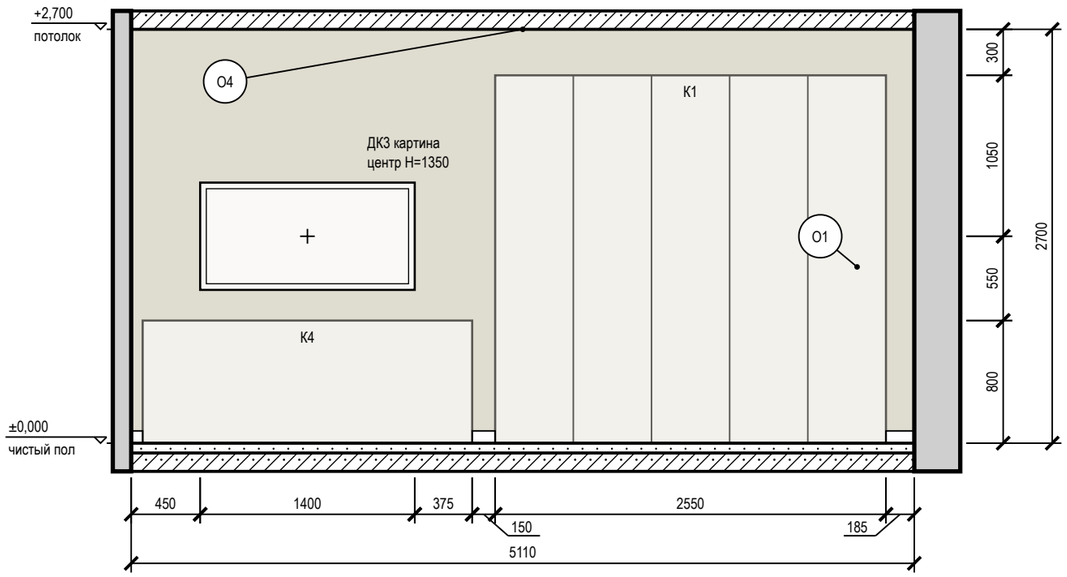


## Схема развёрток (М 1:100)

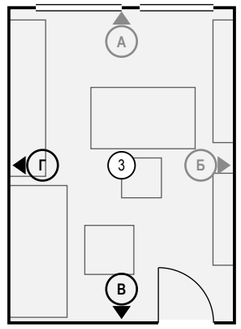


## Условные обозначения

- розетка с заземляющим контактом; у знака — марка, ×N постов в рамке, гр. — группа щита, Н — высота оси, мм
- выключатель одноклавишный
- выключатель двухклавишный (флажков — по числу клавиш)
- выключатель с проходной или перекрёстной клавишей (обратный флажок); тип клавиши — в подписи
- ПК — розетка компьютерная RJ45
- ТВ — розетка телевизионная
- привязки точек и выводов от угла и от пола, мм
- мебель и приборы — фасад по расстановке (условно)
- картина (декор): марка Д, крест — центр, Н — высота центра, мм
- зеркало: марка Д, крест — центр, Н — высота центра, мм
- дверь скрытого монтажа: полотно в плоскости стены (узел — на листе узлов)
- стены и перекрытия в сечении
- окраска: тон — цвет по коду производителя (условно)
- О1 — марка отделки по реестру отделки альбома
- А — марка развёртки: буква стены, стрелка — взгляд

## Ведомость отделки (на листе)

| Марка | Поверхность | Материал, изделие | Цвет, код | Кол. |
|---|---|---|---|---|
| О1 | стены | окраска, Farrow & Ball Modern Emulsion, матовая, подготовка Q3 | Farrow & Ball No. 15 «Bone — мягкий каменно-серый с зеленцой» | 21,8 м² |
| О3 | плинтус | плинтус МДФ, h 80 мм, аналог: плинтус МДФ под покраску 80×16 | Farrow & Ball No. 15 «Bone — мягкий каменно-серый с зеленцой» | 3,2 м |
| О4 | потолок | окраска, Tikkurila Anti-Reflex 2, глубокоматовая, подготовка Q3 | Tikkurila V503 «Winter» | 18,9 м² |

**Допущения и предложения на листе**

Основа листа: размеры сняты с растрового плана заказчика с частичными размерами: рисунок не в масштабе, помещения выровнены по подписанным размерам мебели и проходов; контрольный обмер не выполнен (К-1); высота потолка 2700 мм принята: на плане заказчика её нет (К-2); толщины стен 300 / 120 мм приняты по плану заказчика, не замерены (К-1); разрешённая мощность 15 кВт принята по типовым ТУ для квартиры, ТУ заказчиком не переданы (К-4).

Знак «**» — предложение проектировщика, заказчиком не утверждено (согласовать с заказчиком): записи в реестре нет: Р12 — высота 1100 мм выше нормы 1 м (ПУЭ 6.6.30) по назначению: питание ТВ над комодом, в одной зоне с выводами ТВ2 и LAN2.

См. лист открытых вопросов (лист 6, записи К-1, К-2, К-4).

## Примечания

1. Развёртки — вид на стену изнутри помещения, по часовой стрелке; расположение — на схеме листа и на листе 62; размеры — в мм по чистовым поверхностям; отметки — в м от ±0,000; высоты Н — от чистого пола помещения до оси изделия, у декора — до центра.
2. Красные цепочки — привязки электроточек и выводов: по горизонтали от угла чистовых стен, по вертикали от чистого пола, до оси изделия; звенья короче 3 мм на листе вынесены во второй ярус (ближняя к стене цепочка).
3. У знака электроточки: марка (Р — розетка, S — выключатель, Св — светильник, ЭВ — вывод кабеля), ×N — число постов в рамке, гр. — группа щита, Н — высота оси от чистого пола, мм; группы по клавишам выключателя — на листе выключателей.
4. Схема мебели, приборов и декора не является технической документацией для производства мебели; габариты — по паспортам изделий.
5. Картины и зеркала крепить к основанию по паспорту изделия (закладные и анкеры — в перечне скрытых работ); крест — ось центра предмета.
6. Двери скрытого монтажа — полотно в плоскости стены, отделка стены по полотну, плинтус прерывается у короба (узел — на листе узлов).

1000 мм · печать 1:1

| Изм. | Кол.уч | Лист | № док. | Подп. | Дата |
|---|---|---|---|---|---|
| Разраб. | | Кырлан А.С. | | | 18.10.26 |
| Пров. | | | | | |
| ГИП | | | | | |
| | | | | | |
| Н. контр. | | | | | |
| Утв. | | | | | |

**ГД-2026-008-АИ**

Квартира с кабинетом

Общая площадь 127,29* м² · * размеры со скана, не замерены (реестр — л. 6, К-1)

Дизайн-проект интерьера

| Стадия | Лист | Листов |
|---|---|---|
| РП | 68 | 92 |

**Развёртки стен В, Г. Кабинет (пом. 3)**

М 1:40

**Кырлан Александр Сергеевич**

выпуск 18.10.2026 · d2d5a25dca · стр. 79 из 129

# Развёртка стены Г. Кухня-гостиная (пом. 4), кухонный фронт

Кухня-гостиная (пом. 4) · вид изнутри помещения · размеры в мм, отметки в м

**ПРЕДВАРИТЕЛЬНО · не для производства работ · открыто пунктов: 4 (реестр — л. 6)**

## Развёртка стены Г

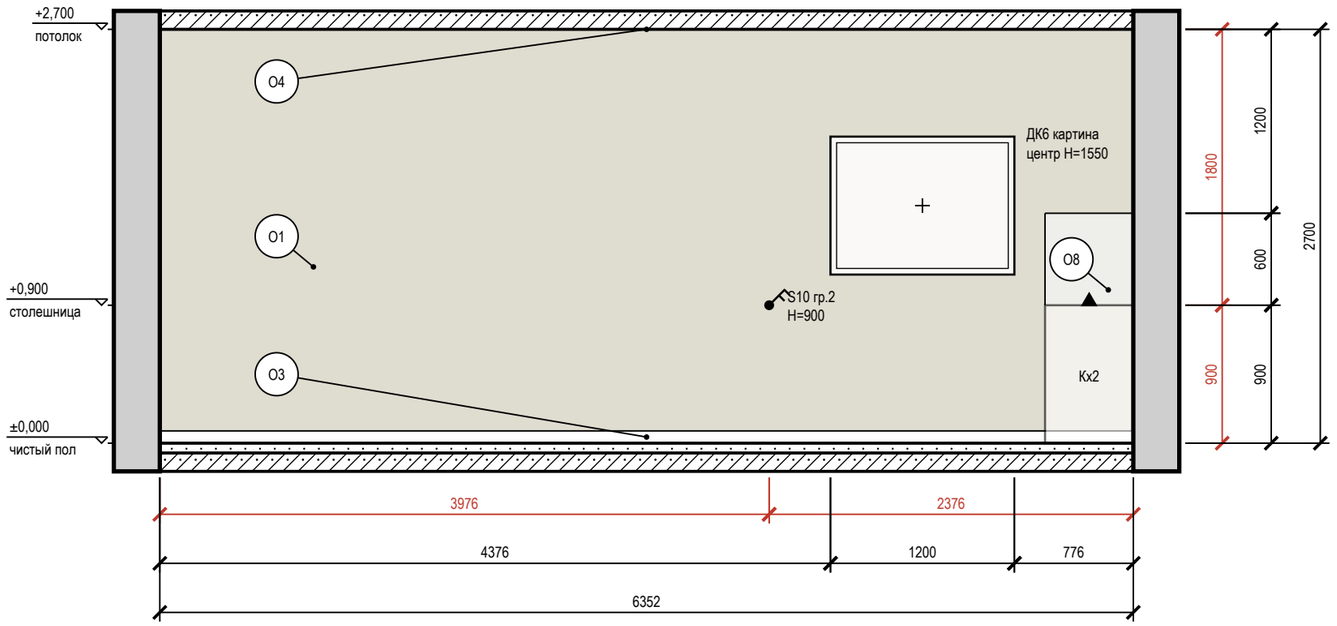


## Условные обозначения

- выключатель одноклавишный
- выключатель двухклавишный (флажков — по числу клавиш)
- привязки точек и выводов от угла и от пола, мм
- мебель и приборы — фасад по расстановке (условно)
- картина (декор): марка Д, крест — центр, Н — высота центра, мм
- стены и перекрытия в сечении
- плитка: сетка швов по формату, ▲ — ось старта
- окраска: тон — цвет по коду производителя (условно)
- О1 — марка отделки по реестру отделки альбома
- А — марка развёртки: буква стены, стрелка — взгляд

## Схема развёрток (М 1:100)

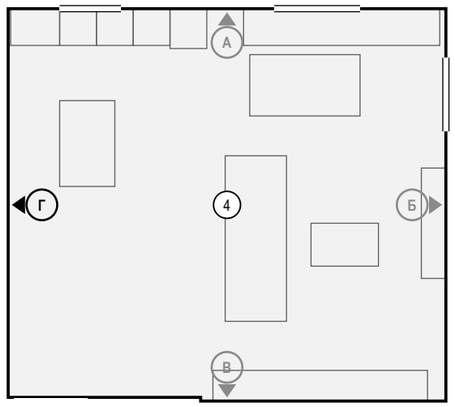


## Ведомость отделки (на листе)

| Марка | Поверхность | Материал, изделие | Цвет, код | Кол. |
|---|---|---|---|---|
| О1 | стены | окраска, Farrow & Ball Modern Emulsion, матовая, подготовка Q3 | Farrow & Ball No. 15 «Bone — мягкий каменно-серый с зеленцой» | 16,8 м² |
| О3 | плинтус | плинтус МДФ, h 80 мм, аналог: плинтус МДФ под покраску 80×16 | Farrow & Ball No. 15 «Bone — мягкий каменно-серый с зеленцой» | 6,4 м |
| О4 | потолок | окраска, Tikkurila Anti-Reflex 2, глубокоматовая, подготовка Q3 | Tikkurila V503 «Winter» | 45,5 м² |
| О8 | фартук | керамогранит, 1200×600×9 мм, аналог: керамогранит под травертин, матовый, затирка CG2WA | | 0,3 м² |

**Допущения и предложения на листе**

Основа листа: размеры сняты с растрового плана заказчика с частичными размерами: рисунок не в масштабе, помещения выровнены по подписанным размерам мебели и проходов; контрольный обмер не выполнен (К-1); высота потолка 2700 мм принята: на плане заказчика её нет (К-2); толщины стен 300 / 120 мм приняты по плану заказчика, не замерены (К-1); разрешённая мощность 15 кВт принята по типовым ТУ для квартиры, ТУ заказчиком не переданы (К-4).

См. лист открытых вопросов (лист 6, записи К-1, К-2, К-4).

## Примечания

1. Развёртки — вид на стену изнутри помещения, по часовой стрелке; расположение — на схеме листа и на листе 62; размеры — в мм по чистовым поверхностям; отметки — в м от ±0,000; высоты Н — от чистого пола помещения до оси изделия, у декора — до центра.
2. Красные цепочки — привязки электроточек и выводов: по горизонтали от угла чистовых стен, по вертикали от чистого пола, до оси изделия; звенья короче 3 мм на листе вынесены во второй ярус (ближняя к стене цепочка).
3. У знака электроточки: марка (Р — розетка, S — выключатель, Св — светильник, ЭВ — вывод кабеля), ×N — число постов в рамке, гр. — группа щита, Н — высота оси от чистого пола, мм; группы по клавишам выключателя — на листе выключателей.
4. Схема мебели, приборов и декора не является технической документацией для производства мебели; габариты — по паспортам изделий.
5. Картины и зеркала крепить к основанию по паспорту изделия (закладные и анкеры — в перечне скрытых работ); крест — ось центра предмета.
6. Высота фартука принята 600 мм над столешницей там, где нет навесных модулей и высота фартука не задана.
7. Выводы кухонной техники — по утверждённому проекту кухни: привязки выводов даются от осей модулей гарнитура.

1000 мм · печать 1:1

| Изм. | Кол.уч | Лист | № док. | Подп. | Дата |
|---|---|---|---|---|---|
| Разраб. | | Кырлан А.С. | | | 18.10.26 |
| Пров. | | | | | |
| ГИП | | | | | |
| | | | | | |
| Н. контр. | | | | | |
| Утв. | | | | | |

**ГД-2026-008-АИ**

Квартира с кабинетом

Общая площадь 127,29* м² · * размеры со скана, не замерены (реестр — л. 6, К-1)

Дизайн-проект интерьера

| Стадия | Лист | Листов |
|---|---|---|
| РП | 69 | 92 |

**Развёртка стены Г. Кухня-гостиная (пом. 4), кухонный фронт**

М 1:40

**Кырлан Александр Сергеевич**

выпуск 18.10.2026 № d2d5a25dca · стр. 80 из 129

# Развёртка стены А. Кухня-гостиная (пом. 4), кухонный фронт

Кухня-гостиная (пом. 4) · вид изнутри помещения · размеры в мм, отметки в м

ПРЕДВАРИТЕЛЬНО · не для производства работ · открыто пунктов: 4 (реестр — л. 6)

## Развёртка стены А

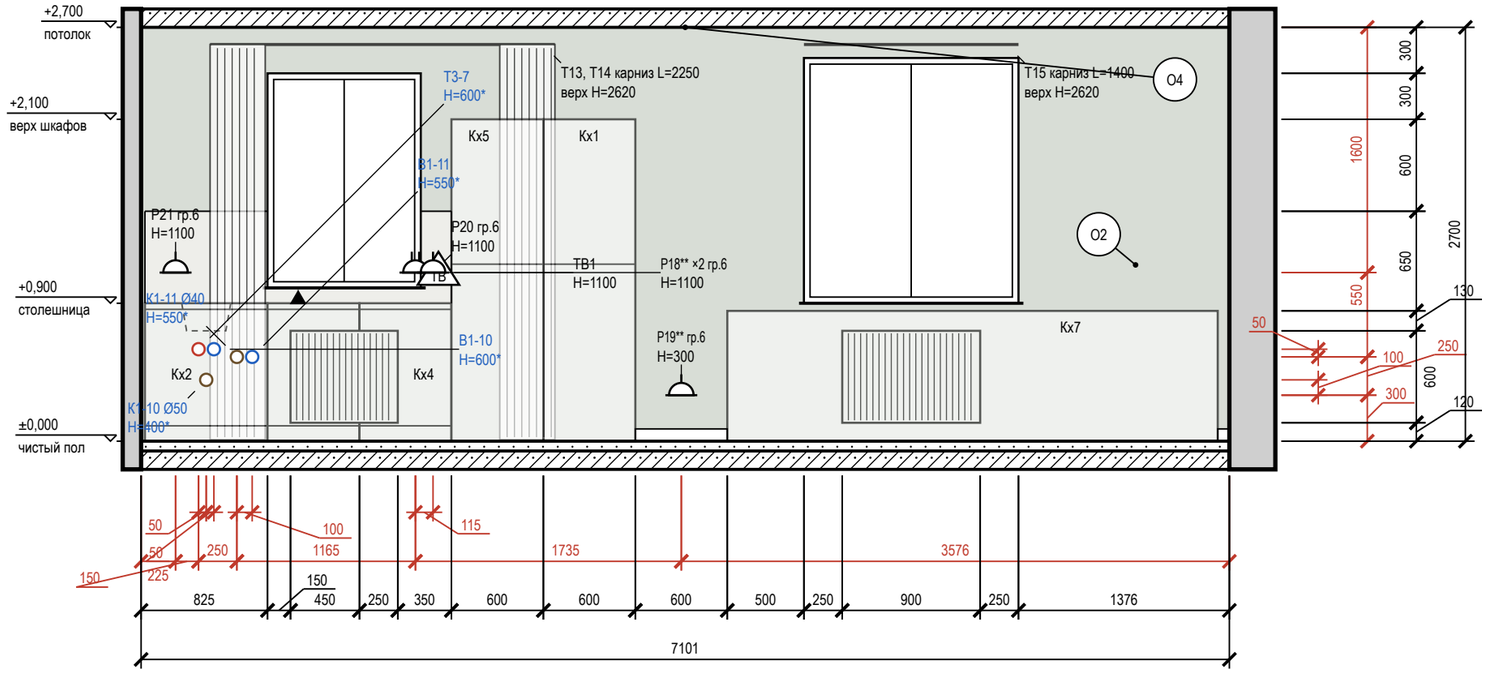


## Ведомость отделки (на листе)

| Марка | Поверхность | Материал, изделие | Цвет, код | Кол. |
|---|---|---|---|---|
| О2 | акцентная стена | окраска, Farrow & Ball Modern Emulsion, матовая, подготовка Q3 | Farrow & Ball No. 34 «Calke Green традиционный шалфей» | 14,3 м² |
| О3 | плинтус | плинтус МДФ, h 80 мм, аналог: плинтус МДФ под покраску 80×16 | Farrow & Ball No. 15 «Bone — мягкий каменно-серый с зеленцой» | 0,7 м |
| О4 | потолок | окраска, Tikkurila Anti-Reflex 2, глубокоматовая, подготовка Q3 | Tikkurila V503 «Winter» | 45,5 м² |
| О8 | фартук | керамогранит, 1200×600×9 мм, аналог: керамогранит под травертин, матовый, затирка CG2WA | | 0,7 м² |

**Допущения и предложения на листе**

Основа листа: размеры сняты с растрового плана заказчика с частичными размерами: рисунок не в масштабе, помещения выровнены по подписанным размерам мебели и проходов; контрольный обмер не выполнен (К-1); высота потолка 2700 мм принята: на плане заказчика её нет (К-2); толщины стен 300 / 120 мм приняты по плану заказчика, не замерены (К-1); разрешённая мощность 15 кВт принята по типовым ТУ для квартиры, ТУ заказчиком не переданы (К-4).

Знак «**» — предложение проектировщика, заказчиком не утверждено (согласовать с заказчиком): записи в реестре нет: Р18 — высота 1100 мм выше нормы 1 м (ПУЭ 6.6.30) по назначению: питание ТВ, в одной зоне с выводами ТВ1 и LAN3; Р19 — высота 1100 мм выше нормы 1 м (ПУЭ 6.6.30) по назначению: питание приставки ТВ, в одной зоне с выводами ТВ1 и LAN3.

См. лист открытых вопросов (лист 6, записи К-1, К-2, К-4).

## Примечания

1. Развёртки — вид на стену изнутри помещения, по часовой стрелке; расположение — на схеме листа и на листе 62; размеры — в мм по чистовым поверхностям; отметки — в м от ±0,000; высоты H — от чистого пола помещения до оси изделия, у декора — до центра.
2. Красные цепочки — привязки электроточек и выводов: по горизонтали от угла чистовых стен, по вертикали от чистого пола, до оси изделия; звенья короче 3 мм на листе вынесены во второй ярус (ближняя к стене цепочка).
3. У знака электроточки: марка (Р — розетка, S — выключатель, Св — светильник, ЭВ — вывод кабеля), ×N — число постов в рамке, гр. — группа щита, H — высота оси от чистого пола, мм; группы по клавишам выключателя — на листе выключателей.
4. Схема мебели, приборов и декора не является технической документацией для производства мебели; габариты — по паспортам изделий.
5. Выводы ВК — коды и высоты по листу выводов сантехники; * — высота принята по типовой практике монтажа, окончательно — по паспорту прибора.
6. Карнизы (шины) — по ведомости текстиля декоратора; длина L и верх H — по развёртке, крепление — до окраски потолка.
7. Высота фартука принята 600 мм над столешницей там, где нет навесных модулей и высота фартука не задана.
8. Выводы кухонной техники — по утверждённому проекту кухни: привязки выводов даются от осей модулей гарнитура.

1000 мм · печать 1:1

## Схема развёрток (М 1:100)

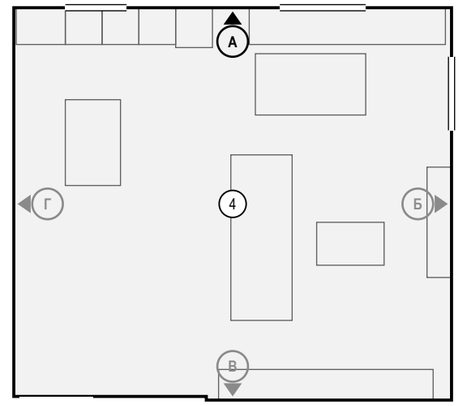


## Условные обозначения

- розетка с заземляющим контактом; у знака — марка, ×N постов в рамке, гр. — группа щита, H — высота оси, мм
- ТВ — розетка телевизионная
- вывод В1 (код — в ведомости привязок)
- вывод Т3 (код — в ведомости привязок)
- вывод К1 (код — в ведомости привязок)
- привязки точек и выводов от угла и от пола, мм
- мебель и приборы — фасад по расстановке (условно)
- карниз (шина) и шторы в собранном виде: марка Т, длина L, верх H
- окно: проём, рама, подоконник
- радиатор отопления; марка — по плану отопления
- стены и перекрытия в сечении
- плитка: сетка швов по формату, ▲ — ось старта
- окраска: тон — цвет по коду производителя (условно)
- О1 — марка отделки по реестру отделки альбома
- А — марка развёртки: буква стены, стрелка — взгляд

| Изм. | Кол.уч | Лист | № док. | Подп. | Дата |
|---|---|---|---|---|---|
| Разраб. | | Кырлан А.С. | | | 18.10.26 |
| Пров. | | | | | |
| ГИП | | | | | |
| | | | | | |
| Н. контр. | | | | | |
| Утв. | | | | | |

**ГД-2026-008-АИ**

Квартира с кабинетом

Общая площадь 127,29* м² · * размеры со скана, не замерены (реестр — л. 6, К-1)

| Дизайн-проект интерьера | Стадия | Лист | Листов |
|---|---|---|---|
| | РП | 70 | 92 |

**Развёртка стены А. Кухня-гостиная (пом. 4), кухонный фронт**

М 1:40

**Кырлан Александр Сергеевич**

выпуск 18.10.2026 № d2d5a25dca · стр. 81 из 129

# Развёртка стены Б. Кухня-гостиная (пом. 4)

Кухня-гостиная (пом. 4) · вид изнутри помещения · размеры в мм, отметки в м

**ПРЕДВАРИТЕЛЬНО · не для производства работ · открыто пунктов: 4 (реестр — л. 6)**

## Развёртка стены Б

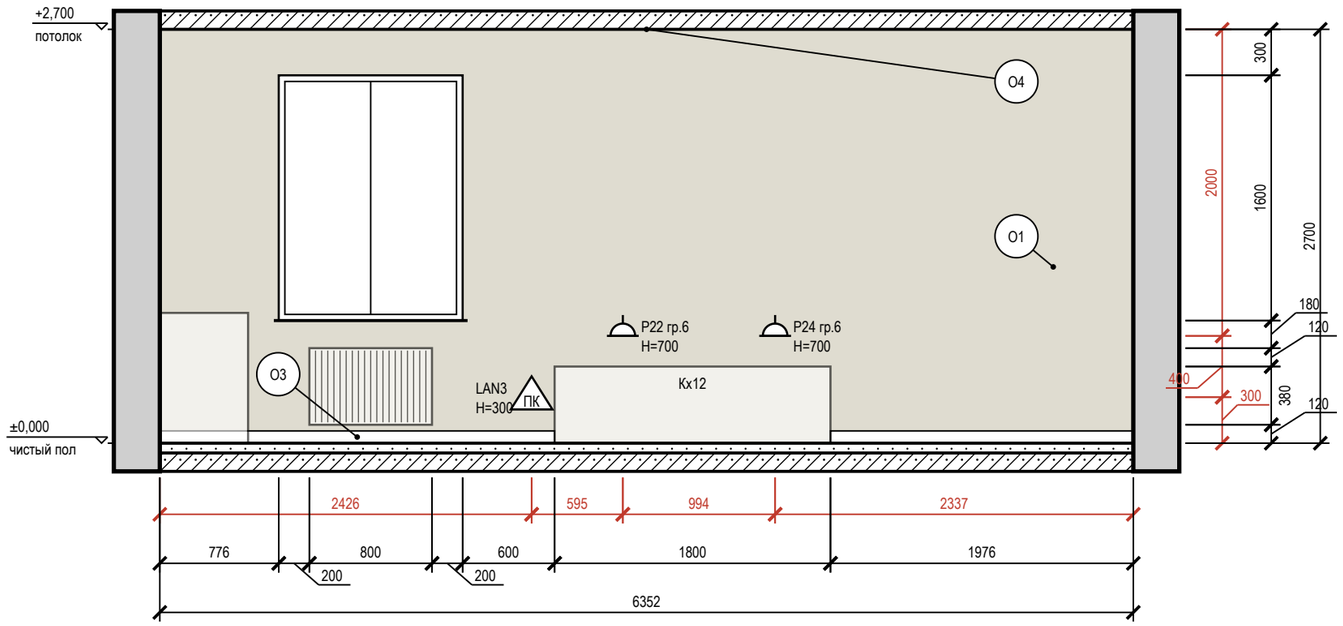


## Условные обозначения

- розетка с заземляющим контактом; у знака — марка, ×N постов в рамке, гр. — группа щита, H — высота оси, мм
- ПК — розетка компьютерная RJ45
- привязки точек и выводов от угла и от пола, мм
- мебель и приборы — фасад по расстановке (условно)
- окно: проём, рама, подоконник
- радиатор отопления; марка — по плану отопления
- стены и перекрытия в сечении
- окраска: тон — цвет по коду производителя (условно)
- О1 — марка отделки по реестру отделки альбома
- A — марка развёртки: буква стены, стрелка — взгляд

## Схема развёрток (М 1:100)

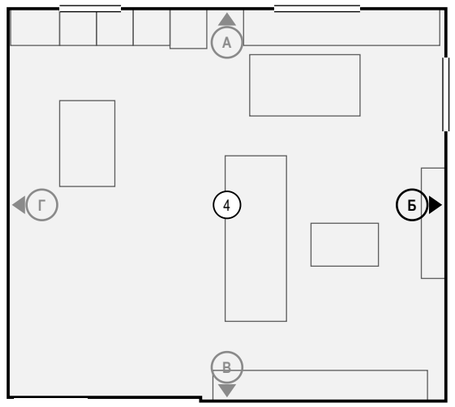


## Ведомость отделки (на листе)

| Марка | Поверхность | Материал, изделие | Цвет, код | Кол. |
|---|---|---|---|---|
| О1 | стены | окраска, Farrow & Ball Modern Emulsion, матовая, подготовка Q3 | Farrow & Ball No. 15 «Bone — мягкий каменно-серый с зеленцой» | 15,2 м² |
| О3 | плинтус | плинтус МДФ, h 80 мм, аналог: плинтус МДФ под покраску 80×16 | Farrow & Ball No. 15 «Bone — мягкий каменно-серый с зеленцой» | 4,6 м |
| О4 | потолок | окраска, Tikkurila Anti-Reflex 2, глубокоматовая, подготовка Q3 | Tikkurila V503 «Winter» | 45,5 м² |

**Допущения и предложения на листе**

Основа листа: размеры сняты с растрового плана заказчика с частичными размерами: рисунок не в масштабе, помещения выровнены по подписанным размерам мебели и проходов; контрольный обмер не выполнен (К-1); высота потолка 2700 мм принята: на плане заказчика её нет (К-2); толщины стен 300 / 120 мм приняты по плану заказчика, не замерены (К-1); разрешённая мощность 15 кВт принята по типовым ТУ для квартиры, ТУ заказчиком не переданы (К-4).

См. лист открытых вопросов (лист 6, записи К-1, К-2, К-4).

## Примечания

1. Развёртки — вид на стену изнутри помещения, по часовой стрелке; расположение — на схеме листа и на листе 62; размеры — в мм по чистовым поверхностям; отметки — в м от ±0,000; высоты H — от чистого пола помещения до оси изделия, у декора — до центра.
2. Красные цепочки — привязки электроточек и выводов: по горизонтали от угла чистовых стен, по вертикали от чистого пола, до оси изделия; звенья короче 3 мм на листе вынесены во второй ярус (ближняя к стене цепочка).
3. У знака электроточки: марка (Р — розетка, S — выключатель, Св — светильник, ЭВ — вывод кабеля), ×N — число постов в рамке, гр. — группа щита, H — высота оси от чистого пола, мм; группы по клавишам выключателя — на листе выключателей.
4. Схема мебели, приборов и декора не является технической документацией для производства мебели; габариты — по паспортам изделий.

1000 мм · печать 1:1

| Изм. | Кол.уч | Лист | № док. | Подп. | Дата |
|---|---|---|---|---|---|
| Разраб. | | Кырлан А.С. | | | 18.10.26 |
| Пров. | | | | | |
| ГИП | | | | | |
| | | | | | |
| Н. контр. | | | | | |
| Утв. | | | | | |

**ГД-2026-008-АИ**

Квартира с кабинетом

Общая площадь 127,29* м² · * размеры со скана, не замерены (реестр — л. 6, К-1)

Дизайн-проект интерьера

| Стадия | Лист | Листов |
|---|---|---|
| РП | 71 | 92 |

**Развёртка стены Б. Кухня-гостиная (пом. 4)**

М 1:40

**Кырлан Александр Сергеевич**

выпуск 18.10.2026 № d2d5a25dca · стр. 82 из 129

# Развёртка стены В. Кухня-гостиная (пом. 4)

Кухня-гостиная (пом. 4) · вид изнутри помещения · размеры в мм, отметки в м

**ПРЕДВАРИТЕЛЬНО · не для производства работ · открыто пунктов: 4 (реестр — л. 6)**

## Развёртка стены В

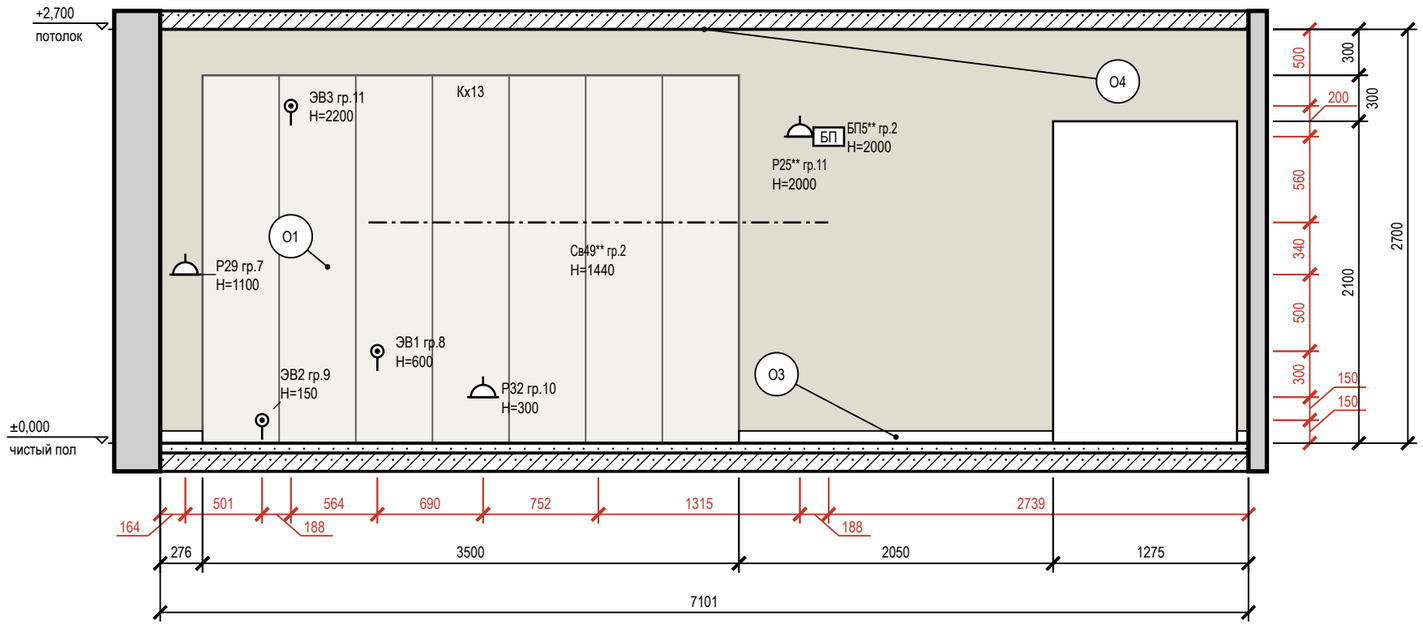


## Условные обозначения

- розетка с заземляющим контактом; у знака — марка, ×N постов в рамке, гр. — группа щита, H — высота оси, мм
- вывод кабеля для подключения прибора (без розетки), марка ЭВ
- светодиодная лента в профиле / в карнизе короба
- БП — блок питания LED, с доступом (люк от 100×100 мм)
- привязки точек и выводов от угла и от пола, мм
- мебель и приборы — фасад по расстановке (условно)
- дверной проём; марка двери — в кружке
- стены и перекрытия в сечении
- окраска: тон — цвет по коду производителя (условно)
- О1 — марка отделки по реестру отделки альбома
- А — марка развёртки: буква стены, стрелка — взгляд

## Схема развёрток (М 1:100)

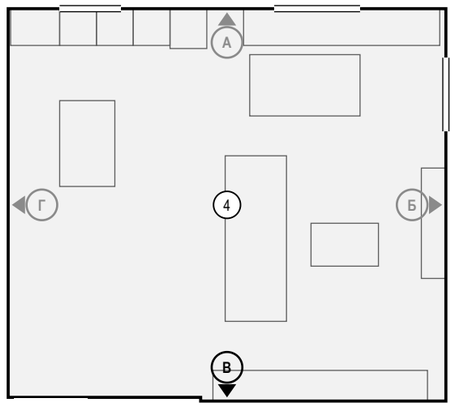


## Ведомость отделки (на листе)

| Марка | Поверхность | Материал, изделие | Цвет, код | Кол. |
|---|---|---|---|---|
| О1 | стены | окраска, Farrow & Ball Modern Emulsion, матовая, подготовка Q3 | Farrow & Ball No. 15 «Bone — мягкий каменно-серый с зеленцой» | 16,7 м² |
| О3 | плинтус | плинтус МДФ, h 80 мм, аналог: плинтус МДФ под покраску 80×16 | Farrow & Ball No. 15 «Bone — мягкий каменно-серый с зеленцой» | 2,4 м |
| О4 | потолок | окраска, Tikkurila Anti-Reflex 2, глубокоматовая, подготовка Q3 | Tikkurila V503 «Winter» | 45,5 м² |

**Допущения и предложения на листе**

Основа листа: размеры сняты с растрового плана заказчика с частичными размерами: рисунок не в масштабе, помещения выровнены по подписанным размерам мебели и проходов; контрольный обмер не выполнен (К-1); высота потолка 2700 мм принята: на плане заказчика её нет (К-2); толщины стен 300 / 120 мм приняты по плану заказчика, не замерены (К-1); разрешённая мощность 15 кВт принята по типовым ТУ для квартиры, ТУ заказчиком не переданы (К-4).

Знак «**» — предложение проектировщика, заказчиком не утверждено (согласовать с заказчиком): записи в реестре нет: Р25 — высота 2000 мм выше нормы 1 м (ПУЭ 6.6.30) по назначению: питание встроенного холодильника М6, розетка над нишей за съёмной панелью; Св49, БП5 — диммируемость добавлена разработчиком проекта под светорегуляторы S11 и S12.

См. лист открытых вопросов (лист 6, записи К-1, К-2, К-4).

## Примечания

1. Развёртки — вид на стену изнутри помещения, по часовой стрелке; расположение — на схеме листа и на листе 62; размеры — в мм по чистовым поверхностям; отметки — в м от ±0,000; высоты H — от чистого пола помещения до оси изделия, у декора — до центра.
2. Красные цепочки — привязки электроточек и выводов: по горизонтали от угла чистовых стен, по вертикали от чистого пола, до оси изделия; звенья короче 3 мм на листе вынесены во второй ярус (ближняя к стене цепочка).
3. У знака электроточки: марка (Р — розетка, S — выключатель, Св — светильник, ЭВ — вывод кабеля), ×N — число постов в рамке, гр. — группа щита, H — высота оси от чистого пола, мм; группы по клавишам выключателя — на листе выключателей.
4. Схема мебели, приборов и декора не является технической документацией для производства мебели; габариты — по паспортам изделий.

1000 мм · печать 1:1

| Изм. | Кол.уч | Лист | № док. | Подп. | Дата |
|---|---|---|---|---|---|
| Разраб. | | Кырлан А.С. | | | 18.10.26 |
| Пров. | | | | | |
| ГИП | | | | | |
| | | | | | |
| Н. контр. | | | | | |
| Утв. | | | | | |

**ГД-2026-008-АИ**

Квартира с кабинетом

Общая площадь 127,29* м² · * размеры со скана, не замерены (реестр — л. 6, К-1)

Дизайн-проект интерьера

| Стадия | Лист | Листов |
|---|---|---|
| РП | 72 | 92 |

**Развёртка стены В. Кухня-гостиная (пом. 4)**

М 1:40

**Кырлан Александр Сергеевич**

выпуск 18.10.2026 № d2d5a25dca · стр. 83 из 129

# Развёртки стен А1, А2. Коридор (пом. 5)

Коридор (пом. 5) · вид изнутри помещения · размеры в мм, отметки в м

**ПРЕДВАРИТЕЛЬНО · не для производства работ · открыто пунктов: 4 (реестр — л. 6)**

## Развёртка стены А1

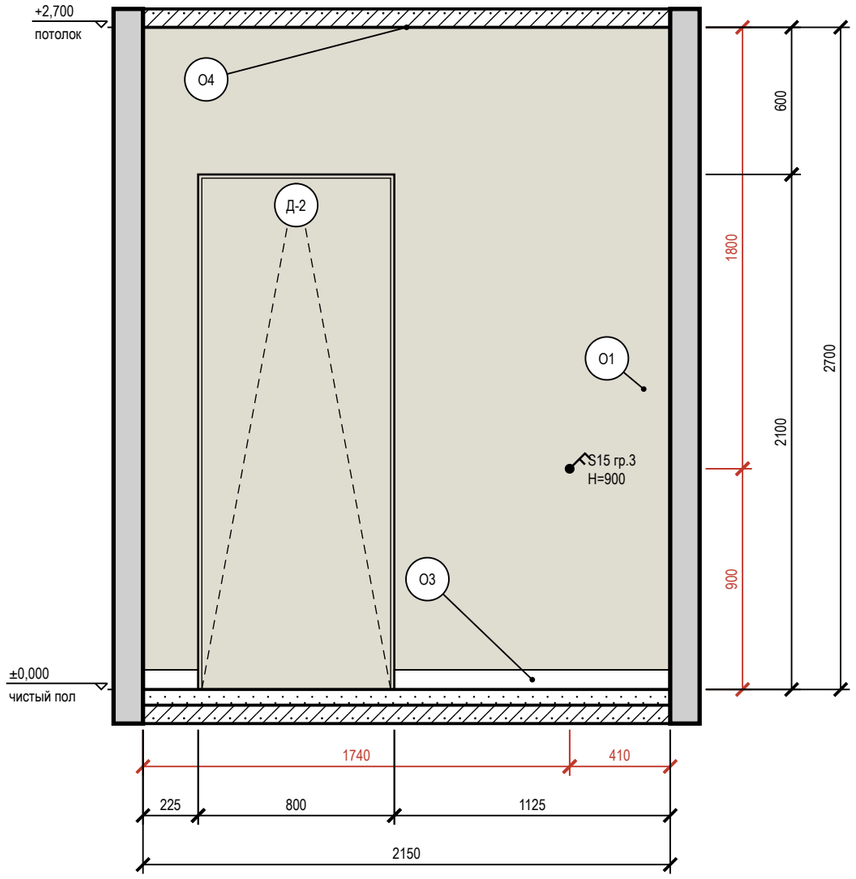


## Развёртка стены А2

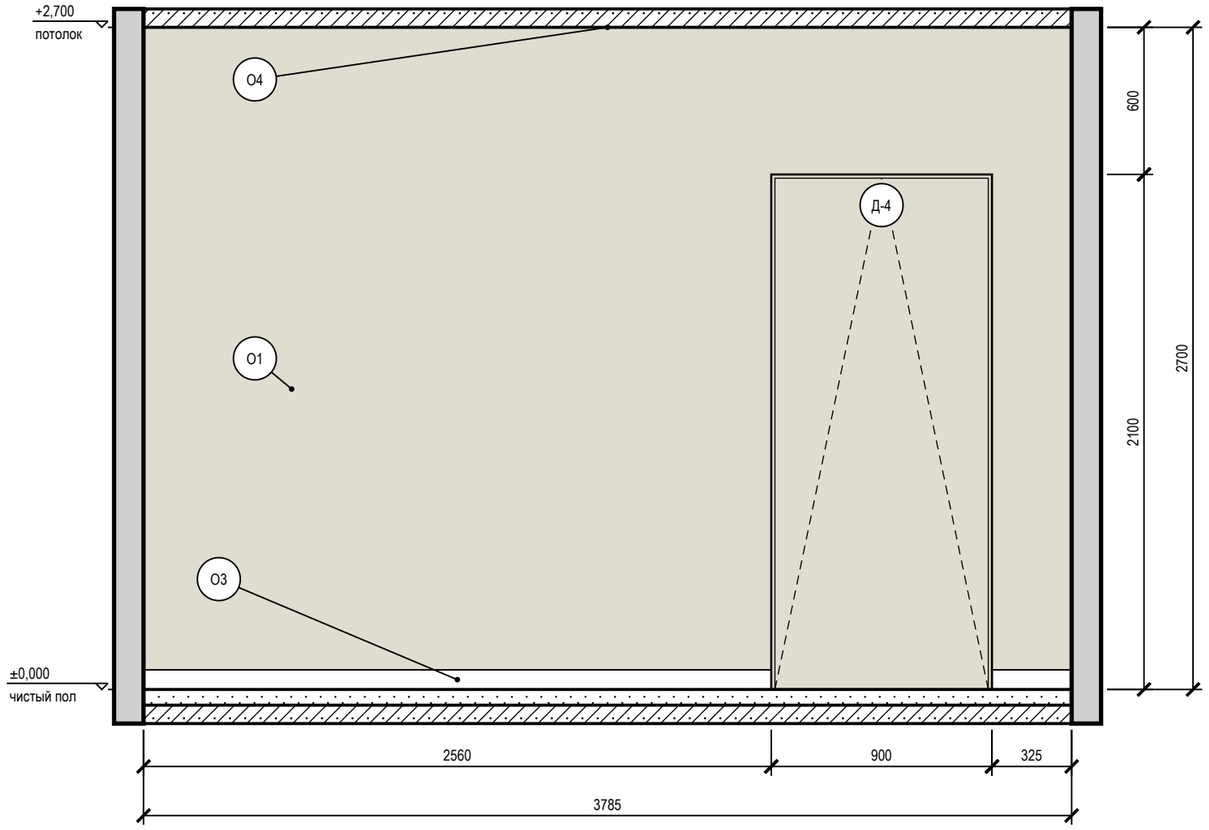


**Допущения и предложения на листе**

Основа листа: размеры сняты с растрового плана заказчика с частичными размерами: рисунок не в масштабе, помещения выровнены по подписанным размерам мебели и проходов; контрольный обмер не выполнен (К-1); высота потолка 2700 мм принята: на плане заказчика её нет (К-2); толщины стен 300 / 120 мм приняты по плану заказчика, не замерены (К-1); разрешённая мощность 15 кВт принята по типовым ТУ для квартиры, ТУ заказчиком не переданы (К-4).

См. лист открытых вопросов (лист 6, записи К-1, К-2, К-4).

## Схема развёрток (М 1:100)

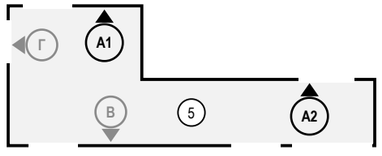


## Условные обозначения

- выключатель одноклавишный
- выключатель двухклавишный (флажков — по числу клавиш)
- привязки точек и выводов от угла и от пола, мм
- мебель и приборы — фасад по расстановке (условно)
- дверь скрытого монтажа: полотно в плоскости стены (узел — на листе узлов)
- стены и перекрытия в сечении
- окраска: тон — цвет по коду производителя (условно)
- О1 — марка отделки по реестру отделки альбома
- А — марка развёртки: буква стены, стрелка — взгляд

## Примечания

1. Развёртки — вид на стену изнутри помещения, по часовой стрелке; расположение — на схеме листа и на листе 62; размеры — в мм по чистовым поверхностям; отметки — в м от ±0,000; высоты Н — от чистого пола помещения до оси изделия, у декора — до центра.
2. Красные цепочки — привязки электроточек и выводов: по горизонтали от угла чистовых стен, по вертикали от чистого пола, до оси изделия; звенья короче 3 мм на листе вынесены во второй ярус (ближняя к стене цепочка).
3. У знака электроточки: марка (Р — розетка, S — выключатель, Св — светильник, ЭВ — вывод кабеля), ×N — число постов в рамке, гр. — группа щита, Н — высота оси от чистого пола, мм; группы по клавишам выключателя — на листе выключателей.
4. Схема мебели, приборов и декора не является технической документацией для производства мебели; габариты — по паспортам изделий.
5. Двери скрытого монтажа — полотно в плоскости стены, отделка стены по полотну, плинтус прерывается у короба (узел — на листе узлов).

1000 мм · печать 1:1

| Изм. | Кол.уч | Лист | № док. | Подп. | Дата |
|---|---|---|---|---|---|
| Разраб. | | Кырлан А.С. | | | 18.10.26 |
| Пров. | | | | | |
| ГИП | | | | | |
| | | | | | |
| Н. контр. | | | | | |
| Утв. | | | | | |

**ГД-2026-008-АИ**

Квартира с кабинетом

Общая площадь 127,29* м² · * размеры со скана, не замерены (реестр — л. 6, К-1)

Дизайн-проект интерьера

| Стадия | Лист | Листов |
|---|---|---|
| РП | 73 | 92 |

**Развёртки стен А1, А2. Коридор (пом. 5)**

М 1:25

**Кырлан Александр Сергеевич**

выпуск 18.10.2026 № d2d5a25dca · стр. 84 из 129

# Развёртки стен В, Г. Коридор (пом. 5)

Коридор (пом. 5) · вид изнутри помещения · размеры в мм, отметки в м

ПРЕДВАРИТЕЛЬНО · не для производства работ · открыто пунктов: 4 (реестр — л. 6)

## Развёртка стены В

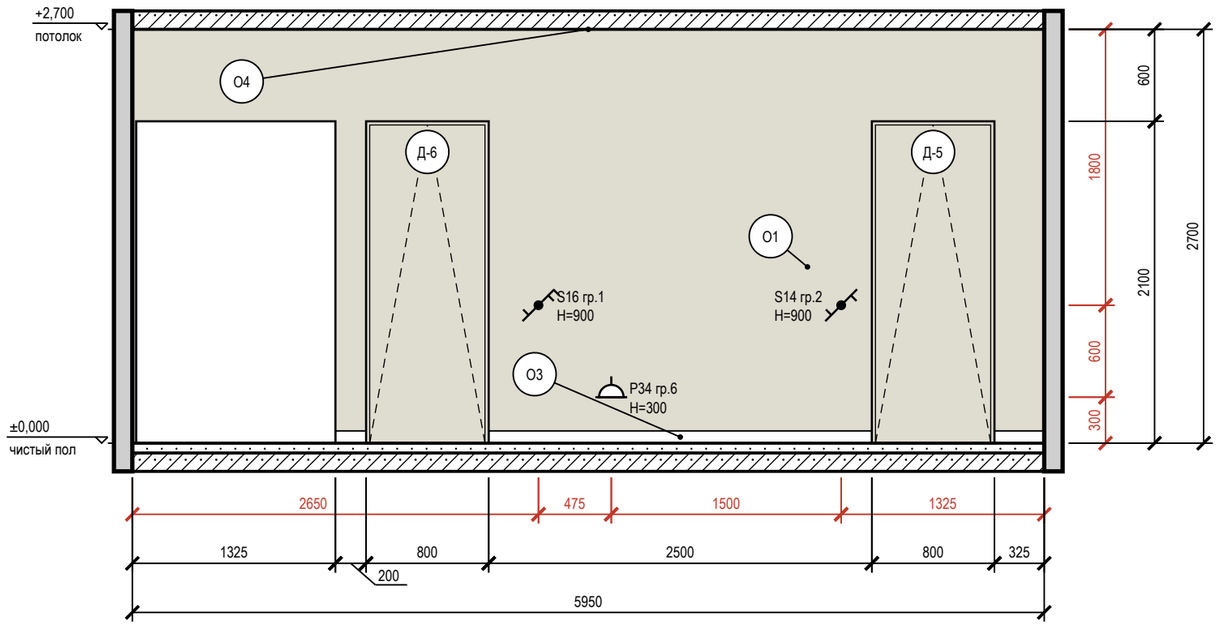


## Развёртка стены Г

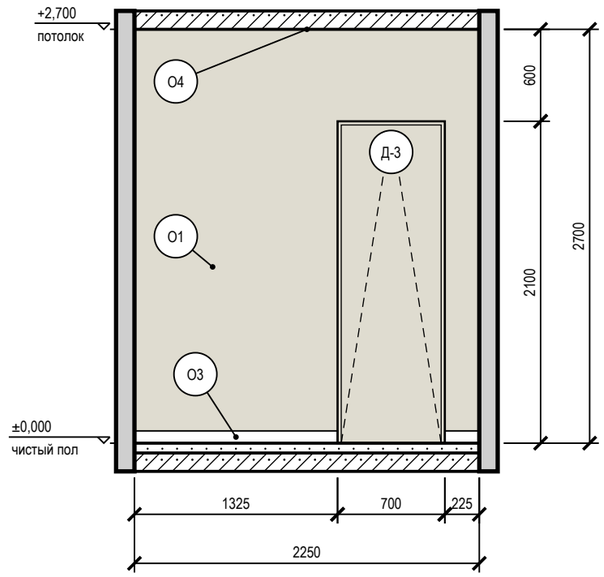


### Схема развёрток (М 1:100)

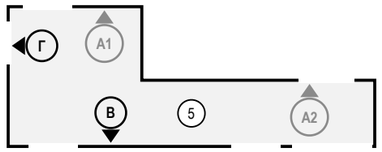


### Условные обозначения

- розетка с заземляющим контактом; у знака — марка, ×N постов в рамке, гр. — группа щита, Н — высота оси, мм
- выключатель одноклавишный
- выключатель двухклавишный (флажков — по числу клавиш)
- выключатель с проходной или перекрёстной клавишей (обратный флажок); тип клавиши — в подписи
- привязки точек и выводов от угла и от пола, мм
- мебель и приборы — фасад по расстановке (условно)
- дверь скрытого монтажа: полотно в плоскости стены (узел — на листе узлов)
- дверной проём; марка двери — в кружке
- стены и перекрытия в сечении
- окраска: тон — цвет по коду производителя (условно)
- О1 — марка отделки по реестру отделки альбома
- А — марка развёртки: буква стены, стрелка — взгляд

### Ведомость отделки (на листе)

| Марка | Поверхность | Материал, изделие | Цвет, код | Кол. |
|---|---|---|---|---|
| О1 | стены | окраска, Farrow & Ball Modern Emulsion, матовая, подготовка Q3 | Farrow & Ball No. 15 «Bone — мягкий каменно-серый с зеленцой» | 14,6 м² |
| О3 | плинтус | плинтус МДФ, h 80 мм, аналог: плинтус МДФ под покраску 80×16 | Farrow & Ball No. 15 «Bone — мягкий каменно-серый с зеленцой» | 4,6 м |
| О4 | потолок | окраска, Tikkurila Anti-Reflex 2, глубокоматовая, подготовка Q3 | Tikkurila V503 «Winter» | 9,1 м² |

**Допущения и предложения на листе**

Основа листа: размеры сняты с растрового плана заказчика с частичными размерами: рисунок не в масштабе, помещения выровнены по подписанным размерам мебели и проходов; контрольный обмер не выполнен (К-1); высота потолка 2700 мм принята: на плане заказчика её нет (К-2); толщины стен 300 / 120 мм приняты по плану заказчика, не замерены (К-1); разрешённая мощность 15 кВт принята по типовым ТУ для квартиры, ТУ заказчиком не переданы (К-4).
См. лист открытых вопросов (лист 6, записи К-1, К-2, К-4).

### Примечания

1. Развёртки — вид на стену изнутри помещения, по часовой стрелке; расположение — на схеме листа и на листе 62; размеры — в мм по чистовым поверхностям; отметки — в м от ±0,000; высоты Н — от чистого пола помещения до оси изделия, у декора — до центра.
2. Красные цепочки — привязки электроточек и выводов: по горизонтали от угла чистовых стен, по вертикали от чистого пола, до оси изделия; звенья короче 3 мм на листе вынесены во второй ярус (ближняя к стене цепочка).
3. У знака электроточки: марка (Р — розетка, S — выключатель, Св — светильник, ЭВ — вывод кабеля), ×N — число постов в рамке, гр. — группа щита, Н — высота оси от чистого пола, мм; группы по клавишам выключателя — на листе выключателей.
4. Схема мебели, приборов и декора не является технической документацией для производства мебели; габариты — по паспортам изделий.
5. Двери скрытого монтажа — полотно в плоскости стены, отделка стены по полотну, плинтус прерывается у короба (узел — на листе узлов).

1000 мм · печать 1:1

| Изм. | Кол.уч | Лист | № док. | Подп. | Дата |
|---|---|---|---|---|---|
| Разраб. | | Кырлан А.С. | | | 18.10.26 |
| Пров. | | | | | |
| ГИП | | | | | |
| | | | | | |
| Н. контр. | | | | | |
| Утв. | | | | | |

**ГД-2026-008-АИ**

Квартира с кабинетом

Общая площадь 127,29* м² · * размеры со скана, не замерены (реестр — л. 6, К-1)

Дизайн-проект интерьера

| Стадия | Лист | Листов |
|---|---|---|
| РП | 74 | 92 |

**Развёртки стен В, Г. Коридор (пом. 5)**

М 1:40

**Кырлан Александр Сергеевич**

выпуск 18.10.2026 · d2d5a25dca · стр. 85 из 129

# Развёртки стен А, Б. Детская (пом. 6)

Детская (пом. 6) · вид изнутри помещения · размеры в мм, отметки в м

ПРЕДВАРИТЕЛЬНО · не для производства работ · открыто пунктов: 4 (реестр — л. 6)

## Развёртка стены А

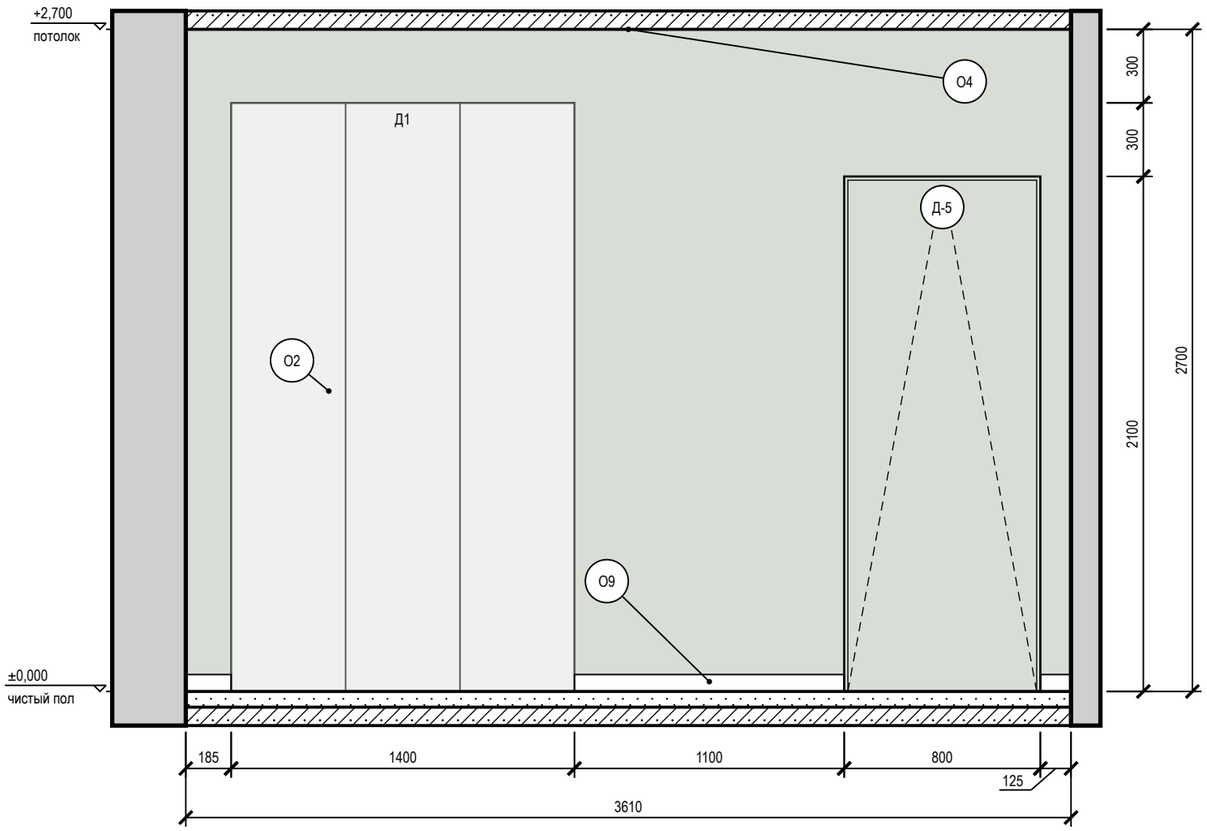


## Развёртка стены Б

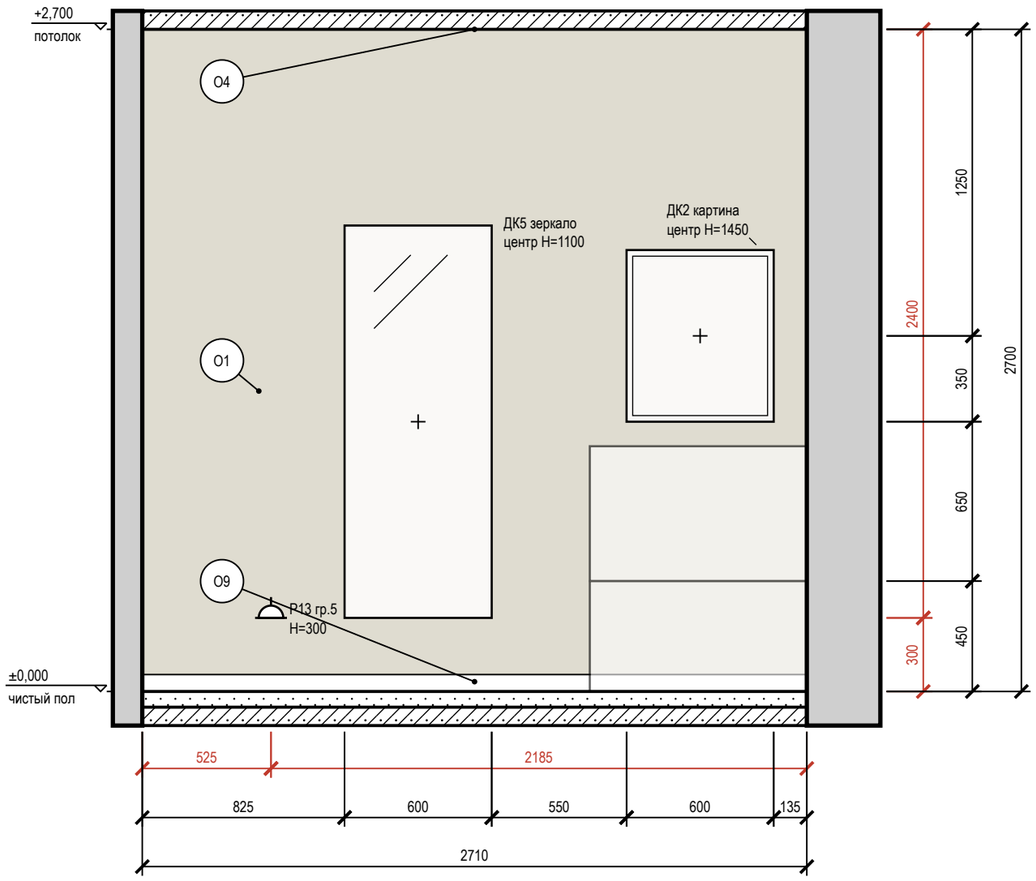


## Схема развёрток (М 1:100)

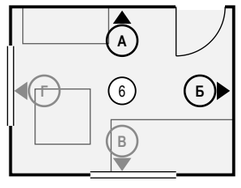


## Условные обозначения

- розетка с заземляющим контактом; у знака — марка, ×N постов в рамке, гр. — группа щита, Н — высота оси, мм
- привязки точек и выводов от угла и от пола, мм
- мебель и приборы — фасад по расстановке (условно)
- картина (декор): марка Д, крест — центр, Н — высота центра, мм
- зеркало: марка Д, крест — центр, Н — высота центра, мм
- дверь скрытого монтажа: полотно в плоскости стены (узел — на листе узлов)
- стены и перекрытия в сечении
- окраска: тон — цвет по коду производителя (условно)
- О1 — марка отделки по реестру отделки альбома
- А — марка развёртки: буква стены, стрелка — взгляд

**Допущения и предложения на листе**

Основа листа: размеры сняты с растрового плана заказчика с частичными размерами: рисунок не в масштабе, помещения выровнены по подписанным размерам мебели и проходов; контрольный обмер не выполнен (К-1); высота потолка 2700 мм принята: на плане заказчика её нет (К-2); толщины стен 300 / 120 мм приняты по плану заказчика, не замерены (К-1); разрешённая мощность 15 кВт принята по типовым ТУ для квартиры, ТУ заказчиком не переданы (К-4).
См. лист открытых вопросов (лист 6, записи К-1, К-2, К-4).

## Примечания

1. Развёртки — вид на стену изнутри помещения, по часовой стрелке; расположение — на схеме листа и на листе 62; размеры — в мм по чистовым поверхностям; отметки — в м от ±0,000; высоты Н — от чистого пола помещения до оси изделия, у декора — до центра.
2. Красные цепочки — привязки электроточек и выводов: по горизонтали от угла чистовых стен, по вертикали от чистого пола, до оси изделия; звенья короче 3 мм на листе вынесены во второй ярус (ближняя к стене цепочка).
3. У знака электроточки: марка (Р — розетка, S — выключатель, Св — светильник, ЭВ — вывод кабеля), ×N — число постов в рамке, гр. — группа щита, Н — высота оси от чистого пола, мм; группы по клавишам выключателя — на листе выключателей.
4. Схема мебели, приборов и декора не является технической документацией для производства мебели; габариты — по паспортам изделий.
5. Картины и зеркала крепить к основанию по паспорту изделия (закладные и анкеры — в перечне скрытых работ); крест — ось центра предмета.
6. Двери скрытого монтажа — полотно в плоскости стены, отделка стены по полотну, плинтус прерывается у короба (узел — на листе узлов).

1000 мм · печать 1:1

| Изм. | Кол.уч | Лист | № док. | Подп. | Дата |
|---|---|---|---|---|---|
| Разраб. | | Кырлан А.С. | | | 18.10.26 |
| Пров. | | | | | |
| ГИП | | | | | |
| | | | | | |
| Н. контр. | | | | | |
| Утв. | | | | | |

**ГД-2026-008-АИ**

Квартира с кабинетом

Общая площадь 127,29* м² · * размеры со скана, не замерены (реестр — л. 6, К-1)

Дизайн-проект интерьера

| Стадия | Лист | Листов |
|---|---|---|
| РП | 75 | 92 |

**Развёртки стен А, Б. Детская (пом. 6)**

М 1:25

**Кырлан Александр Сергеевич**

выпуск 18.10.2026 № d2d5a25dca · стр. 86 из 129

# Развёртки стен В, Г. Детская (пом. 6)

Детская (пом. 6) · вид изнутри помещения · размеры в мм, отметки в м

**ПРЕДВАРИТЕЛЬНО · не для производства работ · открыто пунктов: 4 (реестр — л. 6)**

## Развёртка стены В

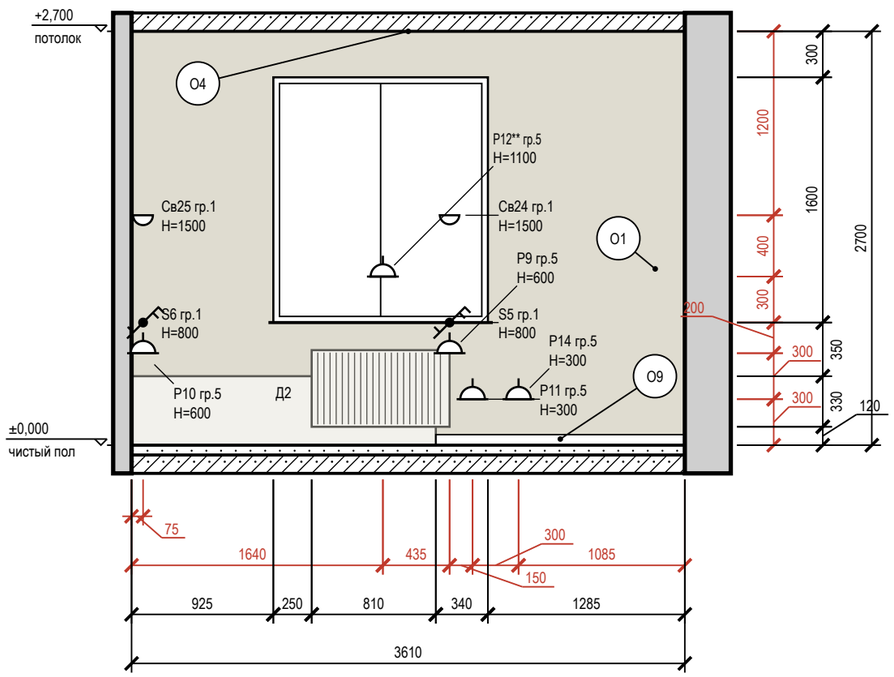


## Развёртка стены Г

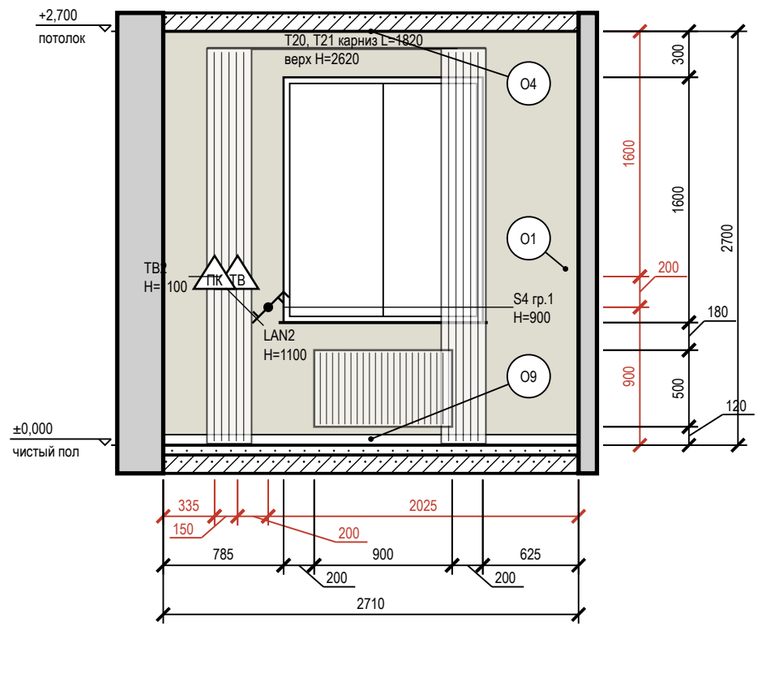


## Условные обозначения

- розетка с заземляющим контактом; у знака — марка, ×N постов в рамке, гр. — группа щита, H — высота оси, мм
- выключатель одноклавишный
- выключатель двухклавишный (флажков — по числу клавиш)
- выключатель с проходной или перекрёстной клавишей (обратный флажок); тип клавиши — в подписи
- светильник настенный (бра), H — высота оси
- ПК — розетка компьютерная RJ45
- ТВ — розетка телевизионная
- привязки точек и выводов от угла и от пола, мм
- мебель и приборы — фасад по расстановке (условно)
- карниз (шина) и шторы в собранном виде: марка T, длина L, верх H
- окно: проём, рама, подоконник
- радиатор отопления; марка — по плану отопления
- стены и перекрытия в сечении
- окраска: тон — цвет по коду производителя (условно)
- О1 — марка отделки по реестру отделки альбома
- A — марка развёртки: буква стены, стрелка — взгляд

## Схема развёрток (М 1:100)

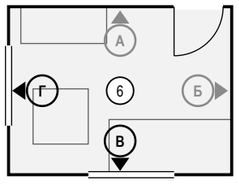


## Ведомость отделки (на листе)

| Марка | Поверхность | Материал, изделие | Цвет, код | Кол. |
|---|---|---|---|---|
| О1 | стены | окраска, Farrow & Ball Modern Emulsion, матовая, подготовка Q3 | Farrow & Ball No. 15 «Bone — мягкий каменно-серый с зеленцой» | 12,7 м² |
| О4 | потолок | окраска, Tikkurila Anti-Reflex 2, глубокоматовая, подготовка Q3 | Tikkurila V503 «Winter» | 10 м² |
| О9 | плинтус | плинтус МДФ, Orac Decor Contour (Luxxus), h 69 мм, SX165 | Farrow & Ball No. 15 «Bone — мягкий каменно-серый с зеленцой» | 4,3 м |

**Допущения и предложения на листе**

Основа листа: размеры сняты с растрового плана заказчика с частичными размерами: рисунок не в масштабе, помещения выровнены по подписанным размерам мебели и проходов; контрольный обмер не выполнен (К-1); высота потолка 2700 мм принята: на плане заказчика её нет (К-2); толщины стен 300 / 120 мм приняты по плану заказчика, не замерены (К-1); разрешённая мощность 15 кВт принята по типовым ТУ для квартиры, ТУ заказчиком не переданы (К-4).

Знак «**» — предложение проектировщика, заказчиком не утверждено (согласовать с заказчиком): записи в реестре нет: Р12 — высота 1100 мм выше нормы 1 м (ПУЭ 6.6.30) по назначению: питание ТВ над комодом, в одной зоне с выводами ТВ2 и LAN2.

См. лист открытых вопросов (лист 6, записи К-1, К-2, К-4).

## Примечания

1. Развёртки — вид на стену изнутри помещения, по часовой стрелке; расположение — на схеме листа и на листе 62; размеры — в мм по чистовым поверхностям; отметки — в м от ±0,000; высоты H — от чистого пола помещения до оси изделия, у декора — до центра.
2. Красные цепочки — привязки электроточек и выводов: по горизонтали от угла чистовых стен, по вертикали от чистого пола, до оси изделия; звенья короче 3 мм на листе вынесены во второй ярус (ближняя к стене цепочка).
3. У знака электроточки: марка (Р — розетка, S — выключатель, Св — светильник, ЭВ — вывод кабеля), ×N — число постов в рамке, гр. — группа щита, H — высота оси от чистого пола, мм; группы по клавишам выключателя — на листе выключателей.
4. Схема мебели, приборов и декора не является технической документацией для производства мебели; габариты — по паспортам изделий.
5. Карнизы (шины) — по ведомости текстиля декоратора; длина L и верх H — по развёртке, крепление — до окраски потолка.

1000 мм · печать 1:1

| Изм. | Кол.уч | Лист | № док. | Подп. | Дата |
|---|---|---|---|---|---|
| Разраб. | | Кырлан А.С. | | | 18.10.26 |
| Пров. | | | | | |
| ГИП | | | | | |
| | | | | | |
| Н. контр. | | | | | |
| Утв. | | | | | |

**ГД-2026-008-АИ**

Квартира с кабинетом

Общая площадь 127,29* м² · * размеры со скана, не замерены (реестр — л. 6, К-1)

| Дизайн-проект интерьера | Стадия | Лист | Листов |
|---|---|---|---|
| | РП | 76 | 92 |

**Развёртки стен В, Г. Детская (пом. 6)**

М 1:40

**Кырлан Александр Сергеевич**

выпуск 18.10.2026 № d2d5a25dca · стр. 87 из 129

# Развёртка стены А. Ванная (пом. 7)

Ванная (пом. 7) · вид изнутри помещения · размеры в мм, отметки в м

**ПРЕДВАРИТЕЛЬНО · не для производства работ · открыто пунктов: 4 (реестр — л. 6)**

## Развёртка стены А

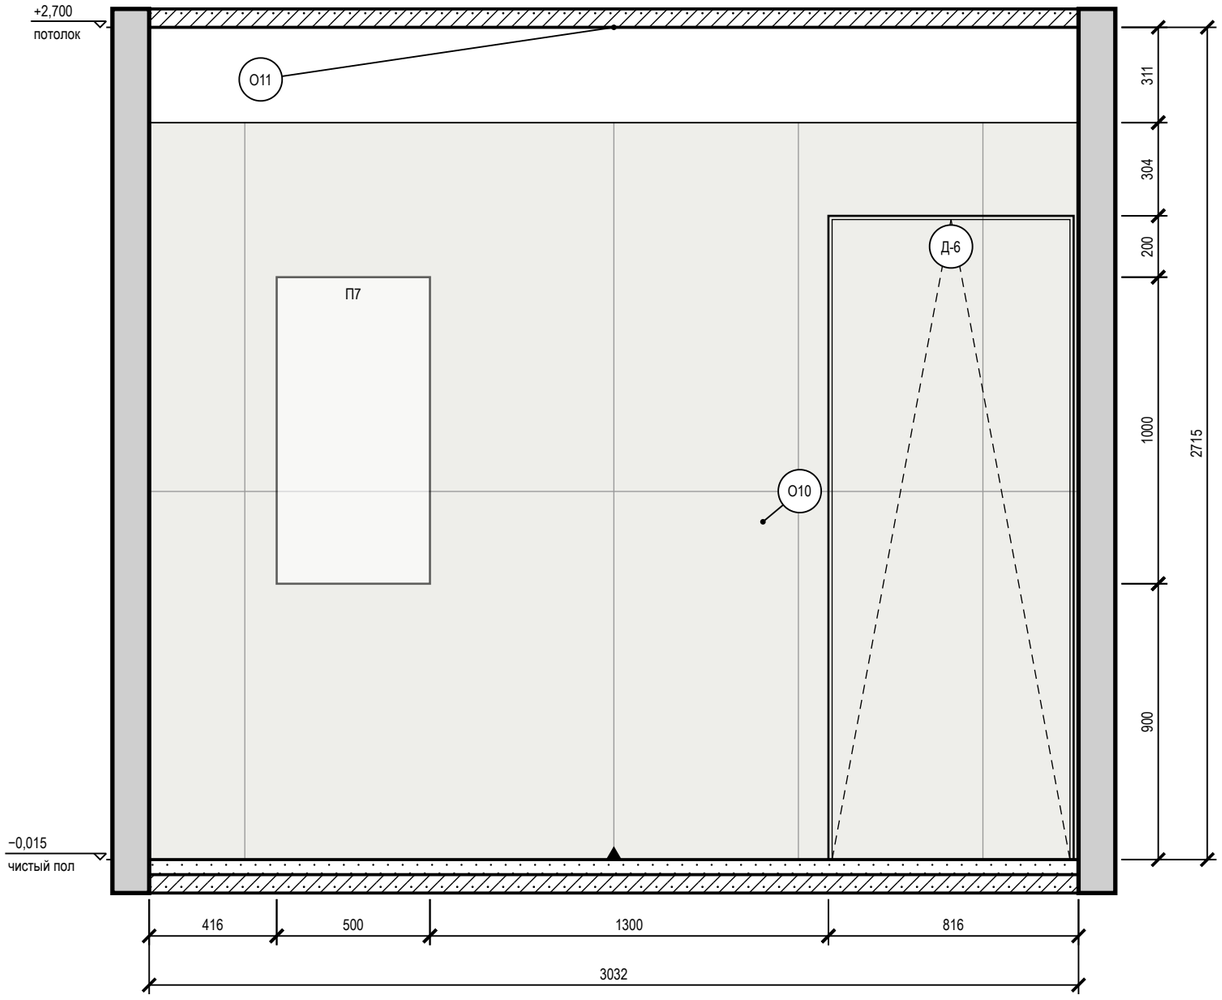


## Схема развёрток (М 1:100)

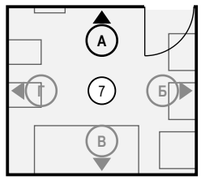


## Условные обозначения

- привязки точек и выводов от угла и от пола, мм
- мебель и приборы — фасад по расстановке (условно)
- дверь скрытого монтажа: полотно в плоскости стены (узел — на листе узлов)
- стены и перекрытия в сечении
- плитка: сетка швов по формату, ▲ — ось старта
- О1 — марка отделки по реестру отделки альбома
- А — марка развёртки: буква стены, стрелка — взгляд

## Ведомость отделки (на листе)

| Марка | Поверхность | Материал, изделие | Цвет, код | Кол. |
|---|---|---|---|---|
| О10 | стены | облицовка плиткой, Atlas Concorde Marvel Travertine, 600×1200×9 мм, A8UZ, затирка CG2WA | Atlas Concorde A8UZ «Marvel Travertine» | 5,6 м² |
| О11 | потолок | окраска, Tikkurila Luja 7, матовая, подготовка Q3 | Tikkurila V503 «Winter» | 8,4 м² |

**Допущения и предложения на листе**

Основа листа: размеры сняты с растрового плана заказчика с частичными размерами: рисунок не в масштабе, помещения выровнены по подписанным размерам мебели и проходов; контрольный обмер не выполнен (К-1); высота потолка 2700 мм принята: на плане заказчика её нет (К-2); толщины стен 300 / 120 мм приняты по плану заказчика, не замерены (К-1); разрешённая мощность 15 кВт принята по типовым ТУ для квартиры, ТУ заказчиком не переданы (К-4).

См. лист открытых вопросов (лист 6, записи К-1, К-2, К-4).

## Примечания

1. Развёртки — вид на стену изнутри помещения, по часовой стрелке; расположение — на схеме листа и на листе 62; размеры — в мм по чистовым поверхностям; отметки — в м от ±0,000; высоты Н — от чистого пола помещения до оси изделия, у декора — до центра.
2. Красные цепочки — привязки электроточек и выводов: по горизонтали от угла чистовых стен, по вертикали от чистого пола, до оси изделия; звенья короче 3 мм на листе вынесены во второй ярус (ближняя к стене цепочка).
3. У знака электроточки: марка (Р — розетка, S — выключатель, Св — светильник, ЭВ — вывод кабеля), ×N — число постов в рамке, гр. — группа щита, Н — высота оси от чистого пола, мм; группы по клавишам выключателя — на листе выключателей.
4. Схема мебели, приборов и декора не является технической документацией для производства мебели; габариты — по паспортам изделий.
5. Облицовка — по сетке швов 2 мм, раскладка от оси стены (треугольник у пола), целые ряды от пола; подрезки — по листу раскладки плитки.
6. Гидроизоляция в 2 слоя, заход на стены 200 мм — до облицовки, с актом скрытых работ и тестом проливом (узел — на листе узлов).
7. Двери скрытого монтажа — полотно в плоскости стены, отделка стены по полотну, плинтус прерывается у короба (узел — на листе узлов).

1000 мм · печать 1:1

| Изм. | Кол.уч | Лист | № док. | Подп. | Дата |
|---|---|---|---|---|---|
| Разраб. | | Кырлан А.С. | | | 18.10.26 |
| Пров. | | | | | |
| ГИП | | | | | |
| | | | | | |
| Н. контр. | | | | | |
| Утв. | | | | | |

**ГД-2026-008-АИ**

Квартира с кабинетом

Общая площадь 127,29* м² · * размеры со скана, не замерены (реестр — л. 6, К-1)

Дизайн-проект интерьера

| Стадия | Лист | Листов |
|---|---|---|
| РП | 77 | 92 |

**Развёртка стены А. Ванная (пом. 7)**

М 1:20

**Кырлан Александр Сергеевич**

выпуск 18.10.2026 № d2d5a25dca · стр. 88 из 129

# Развёртка стены Б. Ванная (пом. 7)

Ванная (пом. 7) · вид изнутри помещения · размеры в мм, отметки в м

**ПРЕДВАРИТЕЛЬНО · не для производства работ · открыто пунктов: 4 (реестр — л. 6)**

## Развёртка стены Б

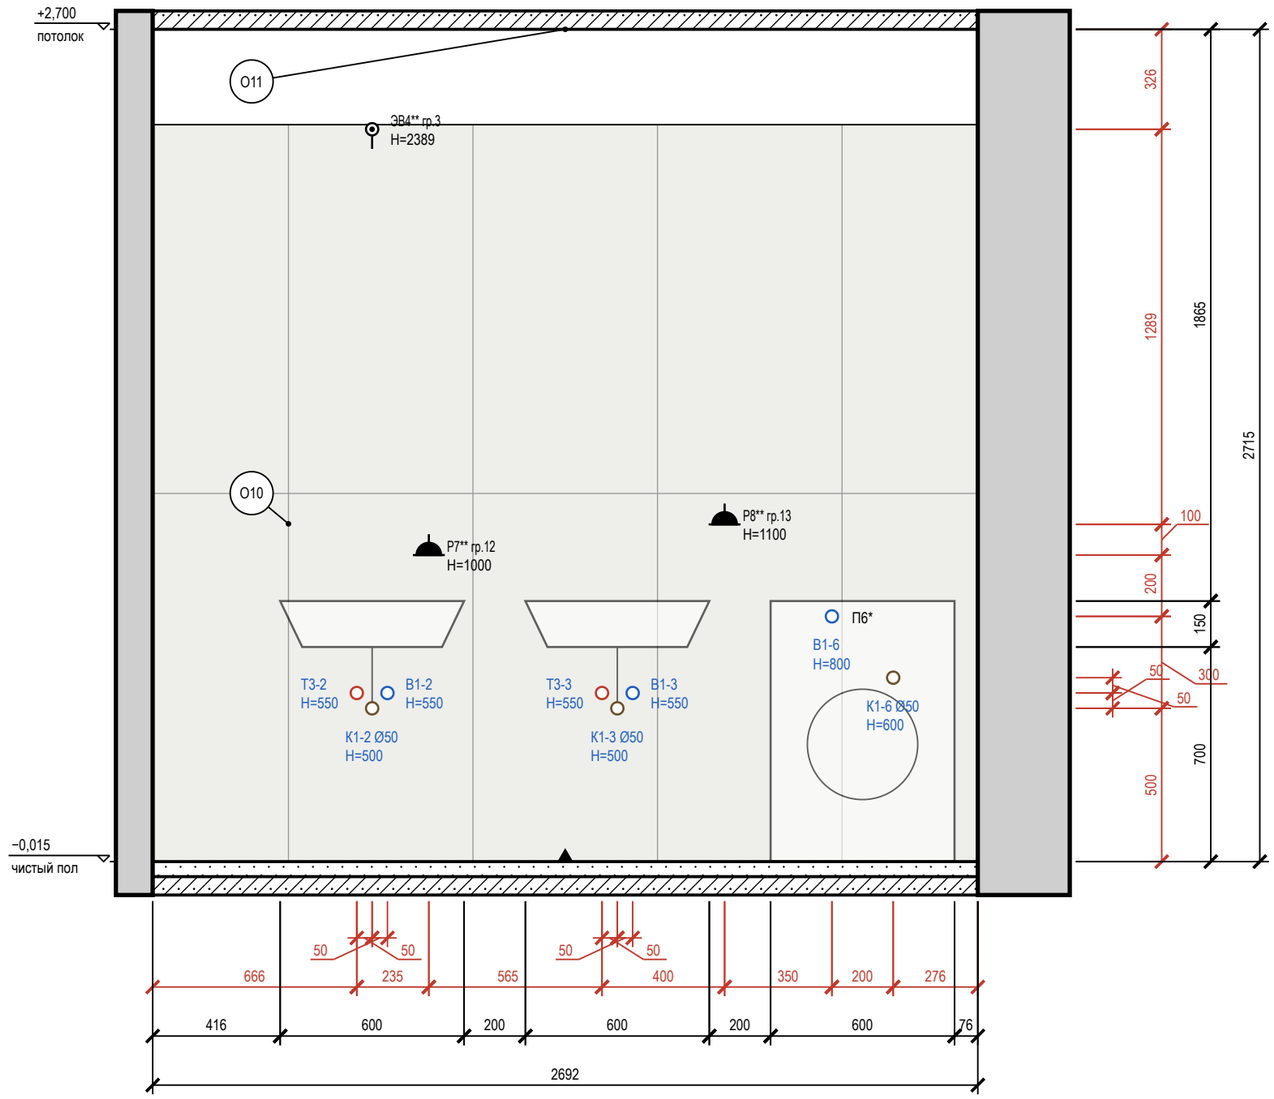


## Схема развёрток (М 1:100)

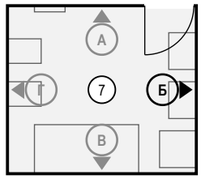


## Условные обозначения

- розетка влагозащищённая IP44
- вывод кабеля для подключения прибора (без розетки), марка ЭВ
- вывод В1 (код — в ведомости привязок)
- вывод Т3 (код — в ведомости привязок)
- вывод К1 (код — в ведомости привязок)
- привязки точек и выводов от угла и от пола, мм
- мебель и приборы — фасад по расстановке (условно)
- стены и перекрытия в сечении
- плитка: сетка швов по формату, ▲ — ось старта
- О1 — марка отделки по реестру отделки альбома
- А — марка развёртки: буква стены, стрелка — взгляд

## Ведомость отделки (на листе)

| Марка | Поверхность | Материал, изделие | Цвет, код | Кол. |
|---|---|---|---|---|
| О10 | стены | облицовка плиткой, Atlas Concorde Marvel Travertine, 600×1200×9 мм, A8UZ, затирка CG2WA | Atlas Concorde A8UZ «Marvel Travertine» | 6,5 м² |
| О11 | потолок | окраска, Tikkurila Luja 7, матовая, подготовка Q3 | Tikkurila V503 «Winter» | 8,4 м² |

**Допущения и предложения на листе**

Основа листа: размеры сняты с растрового плана заказчика с частичными размерами: рисунок не в масштабе, помещения выровнены по подписанным размерам мебели и проходов; контрольный обмер не выполнен (К-1); высота потолка 2700 мм принята: на плане заказчика её нет (К-2); толщины стен 300 / 120 мм приняты по плану заказчика, не замерены (К-1); разрешённая мощность 15 кВт принята по типовым ТУ для квартиры, ТУ заказчиком не переданы (К-4).

Знак «**» — предложение проектировщика, заказчиком не утверждено (согласовать с заказчиком): записи в реестре нет: Р7, Р8 — по образцу: Р7, Р8 и Р33 на высоте 1000 мм — верхний предел нормы (ПУЭ, п. 6.6.30, не выше 1 м); флаг решения снят; ЭВ4 — по образцу: Добавлены выводы к вентиляторам: ЭВ4 (ВР1, ванная) и ЭВ5 (ВР3, санузел 2) — группа 3, высота 2389 мм, включение с основным светом, таймер выбега в вентиляторе; и коробки уравнивания потенциалов КУП1 (ванная) и КУП2 (санузел 2) — высота 300 мм, у входа, вне зон 0–2, проводник от шины РЕ щита ЩК, сече. См. лист открытых вопросов (лист 6, записи К-1, К-2, К-4).

## Примечания

1. Развёртки — вид на стену изнутри помещения, по часовой стрелке; расположение — на схеме листа и на листе 62; размеры — в мм по чистовым поверхностям; отметки — в м от ±0,000; высоты Н — от чистого пола помещения до оси изделия, у декора — до центра.
2. Красные цепочки — привязки электроточек и выводов: по горизонтали от угла чистовых стен, по вертикали от чистого пола, до оси изделия; звенья короче 3 мм на листе вынесены во второй ярус (ближняя к стене цепочка).
3. У знака электроточки: марка (Р — розетка, S — выключатель, Св — светильник, ЭВ — вывод кабеля), ×N — число постов в рамке, гр. — группа щита, Н — высота оси от чистого пола, мм; группы по клавишам выключателя — на листе выключателей.
4. Схема мебели, приборов и декора не является технической документацией для производства мебели; габариты — по паспортам изделий (* — высота не задана в проекте, показана по типовому изделию).
5. Облицовка — по сетке швов 2 мм, раскладка от оси стены (треугольник у пола), целые ряды от пола; подрезки — по листу раскладки плитки.
6. Гидроизоляция в 2 слоя, заход на стены 200 мм — до облицовки, с актом скрытых работ и тестом проливом (узел — на листе узлов).

1000 мм · печать 1:1

| Изм. | Кол.уч | Лист | № док. | Подп. | Дата |
|---|---|---|---|---|---|
| Разраб. | | Кырлан А.С. | | | 18.10.26 |
| Пров. | | | | | |
| ГИП | | | | | |
| | | | | | |
| Н. контр. | | | | | |
| Утв. | | | | | |

**ГД-2026-008-АИ**

Квартира с кабинетом

Общая площадь 127,29* м² · * размеры со скана, не замерены (реестр — л. 6, К-1)

Дизайн-проект интерьера

| Стадия | Лист | Листов |
|---|---|---|
| РП | 78 | 92 |

**Развёртка стены Б. Ванная (пом. 7)**

М 1:20

**Кырлан Александр Сергеевич**

выпуск 18.10.2026 № d2d5a25dca · стр. 89 из 129

# Развёртка стены В. Ванная (пом. 7)

Ванная (пом. 7) · вид изнутри помещения · размеры в мм, отметки в м

**ПРЕДВАРИТЕЛЬНО · не для производства работ · открыто пунктов: 4 (реестр — л. 6)**

## Развёртка стены В

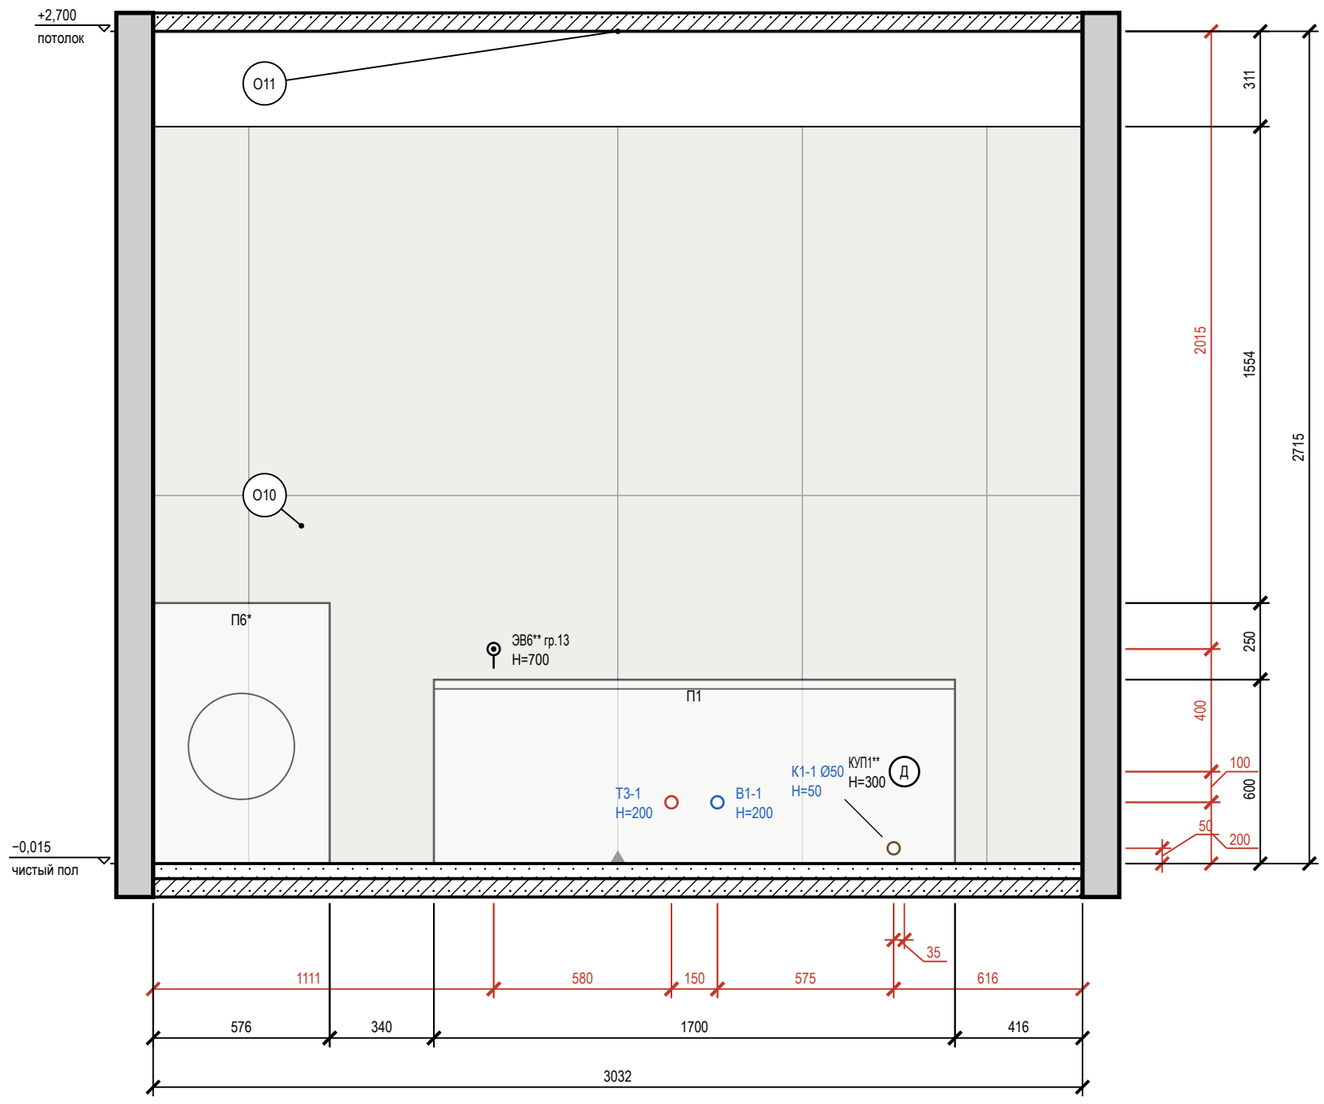


## Схема развёрток (М 1:100)

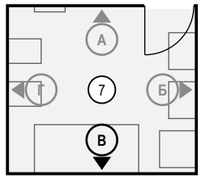


## Условные обозначения

- вывод кабеля для подключения прибора (без розетки), марка ЭВ
- вывод В1 (код — в ведомости привязок)
- вывод Т3 (код — в ведомости привязок)
- вывод К1 (код — в ведомости привязок)
- привязки точек и выводов от угла и от пола, мм
- мебель и приборы — фасад по расстановке (условно)
- стены и перекрытия в сечении
- плитка: сетка швов по формату, ▲ — ось старта
- О1 — марка отделки по реестру отделки альбома
- А — марка развёртки: буква стены, стрелка — взгляд

## Ведомость отделки (на листе)

| Марка | Поверхность | Материал, изделие | Цвет, код | Кол. |
|---|---|---|---|---|
| О10 | стены | облицовка плиткой, Atlas Concorde Marvel Travertine, 600×1200×9 мм, A8UZ, затирка CG2WA | Atlas Concorde A8UZ «Marvel Travertine» | 7,3 м² |
| О11 | потолок | окраска, Tikkurila Luja 7, матовая, подготовка Q3 | Tikkurila V503 «Winter» | 8,4 м² |

Допущения и предложения на листе. Основа листа: размеры сняты с растрового плана заказчика с частичными размерами: рисунок не в масштабе, помещения выровнены по подписанным размерам мебели и проходов; контрольный обмер не выполнен (К-1); высота потолка 2700 мм принята: на плане заказчика её нет (К-2); толщины стен 300 / 120 мм приняты по плану заказчика, не замерены (К-1); разрешённая мощность 15 кВт принята по типовым ТУ для квартиры, ТУ заказчиком не переданы (К-4). Знак «**» — предложение проектировщика, заказчиком не утверждено (согласовать с заказчиком): записи в реестре нет: КУП1 — по образцу: Добавлены выводы к вентиляторам: ЭВ4 (ВР1, ванная) и ЭВ5 (ВР3, санузел 2) — группа 3, высота 2389 мм, включение с основным светом, таймер выбега в вентиляторе; и коробки уравнивания потенциалов КУП1 (ванная) и КУП2 (санузел 2) — высота 300 мм, у входа, вне зон 0–2, проводник от шины PE щита ЩК, сече; ЭВ6 — по образцу: Добавлены электрические полотенцесушители IP44: П10 в ванной (480 мм, низ 900 мм) и П13 в санузле 2 (400 мм, низ 900 мм), выводы ЭВ6 и ЭВ7; мощность группы 13 — 2,4 кВт вместо 1,8 кВт. См. лист открытых вопросов (лист 6, записи К-1, К-2, К-4).

## Примечания

1. Развёртки — вид на стену изнутри помещения, по часовой стрелке; расположение — на схеме листа и на листе 62; размеры — в мм по чистовым поверхностям; отметки — в м от ±0,000; высоты Н — от чистого пола помещения до оси изделия, у декора — до центра.
2. Красные цепочки — привязки электроточек и выводов: по горизонтали от угла чистовых стен, по вертикали от чистого пола, до оси изделия; звенья короче 3 мм на листе вынесены во второй ярус (ближняя к стене цепочка).
3. У знака электроточки: марка (Р — розетка, S — выключатель, Св — светильник, ЭВ — вывод кабеля), ×N — число постов в рамке, гр. — группа щита, Н — высота оси от чистого пола, мм; группы по клавишам выключателя — на листе выключателей.
4. Схема мебели, приборов и декора не является технической документацией для производства мебели; габариты — по паспортам изделий (* — высота не задана в проекте, показана по типовому изделию).
5. Облицовка — по сетке швов 2 мм, раскладка от оси стены (треугольник у пола), целые ряды от пола; подрезки — по листу раскладки плитки.
6. Гидроизоляция в 2 слоя, заход на стены 200 мм — до облицовки, с актом скрытых работ и тестом проливом (узел — на листе узлов).

1000 мм · печать 1:1

| Изм. | Кол.уч | Лист | № док. | Подп. | Дата |
|---|---|---|---|---|---|
| Разраб. | | Кырлан А.С. | | | 18.10.26 |
| Пров. | | | | | |
| ГИП | | | | | |
| | | | | | |
| Н. контр. | | | | | |
| Утв. | | | | | |

**ГД-2026-008-АИ**

Квартира с кабинетом

Общая площадь 127,29* м² · * размеры со скана, не замерены (реестр — л. 6, К-1)

| Дизайн-проект интерьера | Стадия | Лист | Листов |
|---|---|---|---|
| | РП | 79 | 92 |

**Развёртка стены В. Ванная (пом. 7)**

М 1:20

**Кырлан Александр Сергеевич**

выпуск 18.10.2026 № d2d5a25dca · стр. 90 из 129

# Развёртка стены Г. Ванная (пом. 7)

Ванная (пом. 7) · вид изнутри помещения · размеры в мм, отметки в м

ПРЕДВАРИТЕЛЬНО · не для производства работ · открыто пунктов: 4 (реестр — л. 6)

## Развёртка стены Г

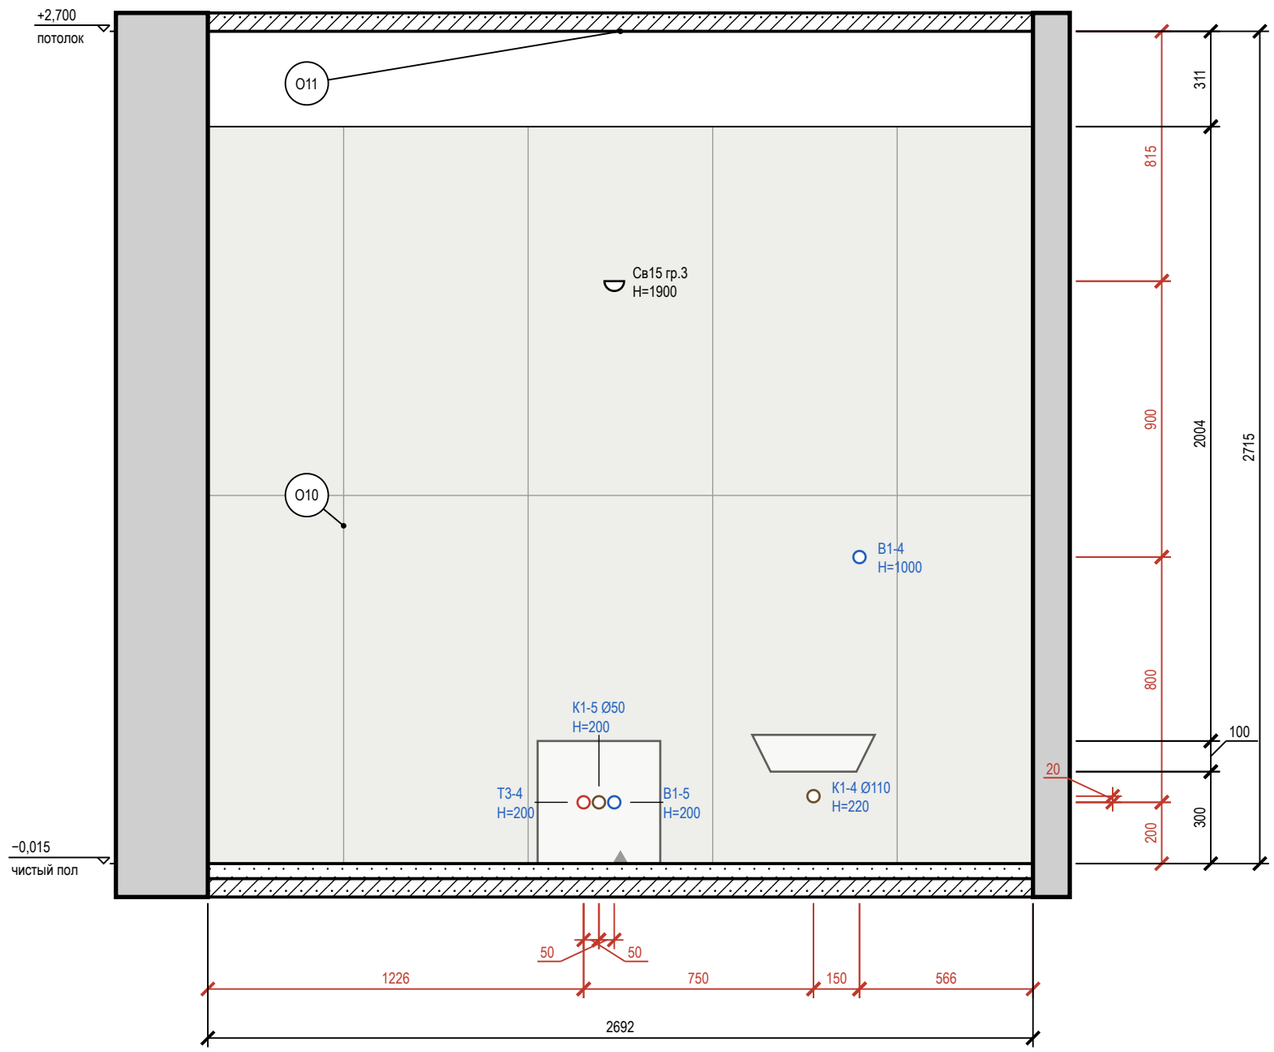


## Схема развёрток (М 1:100)

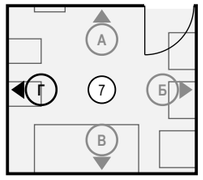


## Условные обозначения

- светильник настенный (бра), H — высота оси
- вывод В1 (код — в ведомости привязок)
- вывод Т3 (код — в ведомости привязок)
- вывод К1 (код — в ведомости привязок)
- привязки точек и выводов от угла и от пола, мм
- мебель и приборы — фасад по расстановке (условно)
- стены и перекрытия в сечении
- плитка: сетка швов по формату, ▲ — ось старта
- О1 — марка отделки по реестру отделки альбома
- А — марка развёртки: буква стены, стрелка — взгляд

## Ведомость отделки (на листе)

| Марка | Поверхность | Материал, изделие | Цвет, код | Кол. |
|---|---|---|---|---|
| О10 | стены | облицовка плиткой, Atlas Concorde Marvel Travertine, 600×1200×9 мм, A8UZ, затирка CG2WA | Atlas Concorde A8UZ «Marvel Travertine» | 6,5 м² |
| О11 | потолок | окраска, Tikkurila Luja 7, матовая, подготовка Q3 | Tikkurila V503 «Winter» | 8,4 м² |

**Допущения и предложения на листе**

Основа листа: размеры сняты с растрового плана заказчика с частичными размерами: рисунок не в масштабе, помещения выровнены по подписанным размерам мебели и проходов; контрольный обмер не выполнен (К-1); высота потолка 2700 мм принята: на плане заказчика её нет (К-2); толщины стен 300 / 120 мм приняты по плану заказчика, не замерены (К-1); разрешённая мощность 15 кВт принята по типовым ТУ для квартиры, ТУ заказчиком не переданы (К-4).

См. лист открытых вопросов (лист 6, записи К-1, К-2, К-4).

## Примечания

1. Развёртки — вид на стену изнутри помещения, по часовой стрелке; расположение — на схеме листа и на листе 62; размеры — в мм по чистовым поверхностям; отметки — в м от ±0,000; высоты H — от чистого пола помещения до оси изделия, у декора — до центра.
2. Красные цепочки — привязки электроточек и выводов: по горизонтали от угла чистовых стен, по вертикали от чистого пола, до оси изделия; звенья короче 3 мм на листе вынесены во второй ярус (ближняя к стене цепочка).
3. У знака электроточки: марка (Р — розетка, S — выключатель, Св — светильник, ЭВ — вывод кабеля), ×N — число постов в рамке, гр. — группа щита, H — высота оси от чистого пола, мм; группы по клавишам выключателя — на листе выключателей.
4. Схема мебели, приборов и декора не является технической документацией для производства мебели; габариты — по паспортам изделий (* — высота не задана в проекте, показана по типовому изделию).
5. Облицовка — по сетке швов 2 мм, раскладка от оси стены (треугольник у пола), целые ряды от пола; подрезки — по листу раскладки плитки.
6. Гидроизоляция в 2 слоя, заход на стены 200 мм — до облицовки, с актом скрытых работ и тестом проливом (узел — на листе узлов).

1000 мм · печать 1:1

| Изм. | Кол.уч | Лист | № док. | Подп. | Дата |
|---|---|---|---|---|---|
| Разраб. | | Кырлан А.С. | | | 18.10.26 |
| Пров. | | | | | |
| ГИП | | | | | |
| Н. контр. | | | | | |
| Утв. | | | | | |

**ГД-2026-008-АИ**

Квартира с кабинетом

Общая площадь 127,29* м² · * размеры со скана, не замерены (реестр — л. 6, К-1)

| Дизайн-проект интерьера | Стадия | Лист | Листов |
|---|---|---|---|
| | РП | 80 | 92 |

**Развёртка стены Г. Ванная (пом. 7)**

М 1:20

**Кырлан Александр Сергеевич**

выпуск 18.10.2026 № d2d5a25dca · стр. 91 из 129

# Развёртки стен. Прихожая (пом. 8)

Прихожая (пом. 8) · вид изнутри помещения · размеры в мм, отметки в м

ПРЕДВАРИТЕЛЬНО · не для производства работ · открыто пунктов: 4 (реестр — л. 6)

## Развёртка стены Б

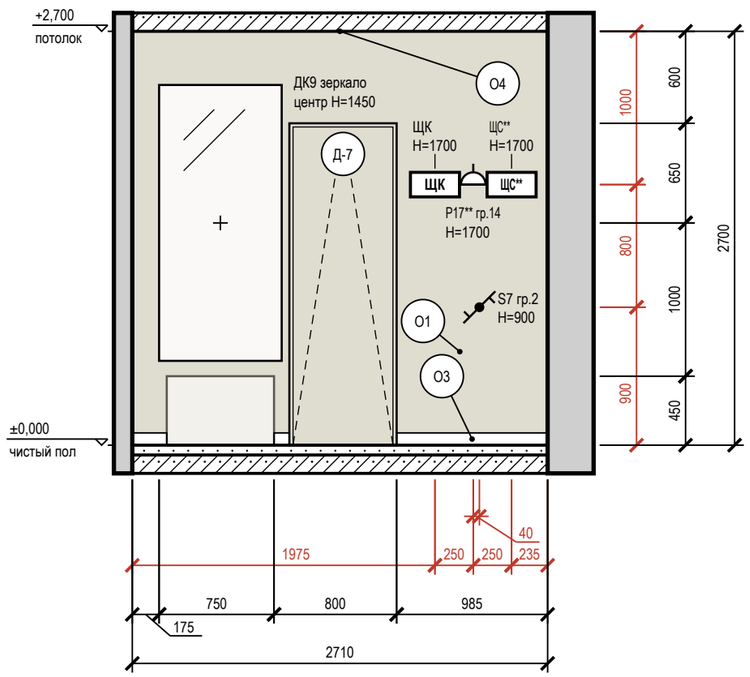


## Развёртка стены В

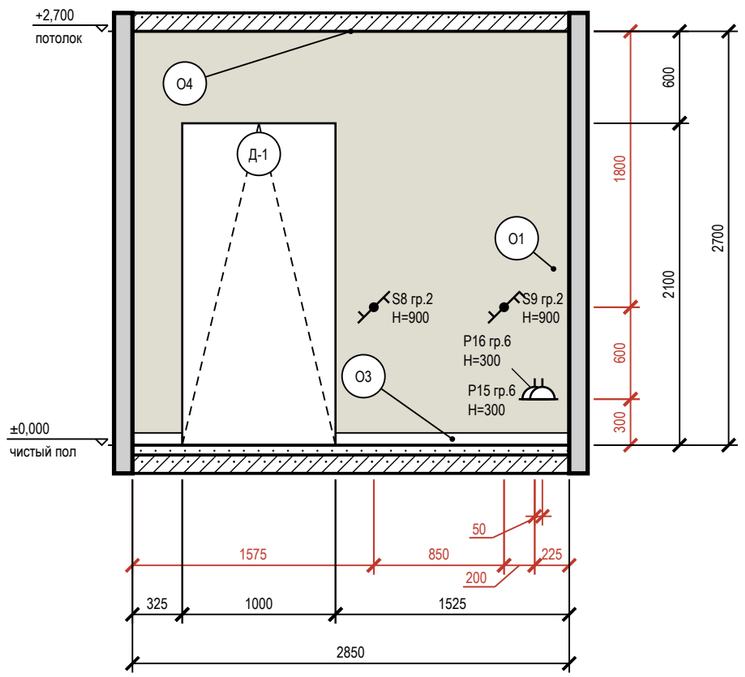


## Развёртка стены Г

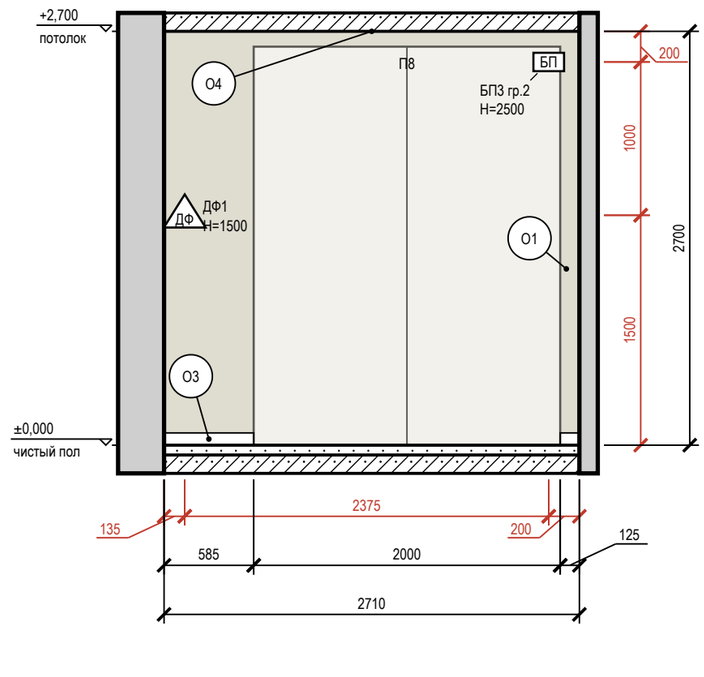


## Схема развёрток (М 1:100)

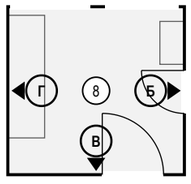


## Условные обозначения

- розетка с заземляющим контактом; у знака — марка, ×N постов в рамке, гр. — группа щита, Н — высота оси, мм
- выключатель одноклавишный
- выключатель двухклавишный (флажков — по числу клавиш)
- выключатель с проходной или перекрёстной клавишей (обратный флажок); тип клавиши — в подписи
- БП — блок питания LED, с доступом (люк от 100×100 мм)
- ДФ — трубка или монитор домофона
- ЩК — щит квартирный
- привязки точек и выводов от угла и от пола, мм
- мебель и приборы — фасад по расстановке (условно)
- зеркало: марка Д, крест — центр, Н — высота центра, мм
- дверь скрытого монтажа: полотно в плоскости стены (узел — на листе узлов)
- дверной проём; марка двери — в кружке
- стены и перекрытия в сечении
- окраска: тон — цвет по коду производителя (условно)
- О1 — марка отделки по реестру отделки альбома
- А — марка развёртки: буква стены, стрелка — взгляд

## Ведомость отделки (на листе)

| Марка | Поверхность | Материал, изделие | Цвет, код | Кол. |
|---|---|---|---|---|
| О1 | стены | окраска, Farrow & Ball Modern Emulsion, матовая, подготовка Q3 | Farrow & Ball No. 15 «Bone — мягкий каменно-серый с зеленцой» | 18,8 м² |
| О3 | плинтус | плинтус МДФ, h 80 мм, аналог: плинтус МДФ под покраску 80×16 | Farrow & Ball No. 15 «Bone — мягкий каменно-серый с зеленцой» | 3,9 м |
| О4 | потолок | окраска, Tikkurila Anti-Reflex 2, глубокоматовая, подготовка Q3 | Tikkurila V503 «Winter» | 7,9 м² |

**Допущения и предложения на листе**

Основа листа: размеры сняты с растрового плана заказчика с частичными размерами: рисунок не в масштабе, помещения выровнены по подписанным размерам мебели и проходов; контрольный обмер не выполнен (К-1); высота потолка 2700 мм принята: на плане заказчика её нет (К-2); толщины стен 300 / 120 мм приняты по плану заказчика, не замерены (К-1); разрешённая мощность 15 кВт принята по типовым ТУ для квартиры, ТУ заказчиком не переданы (К-4).

Знак «**» — предложение проектировщика, заказчиком не утверждено (согласовать с заказчиком): записи в реестре нет: Р17 — высота 1700 мм выше нормы 1 м (ПУЭ 6.6.30) по назначению: питание слаботочного щита ЩС, рядом со щитом на его высоте; ЩС — щит слаботочный: место и состав.

См. лист открытых вопросов (лист 6, записи К-1, К-2, К-4).

## Примечания

1. Развёртки — вид на стену изнутри помещения, по часовой стрелке; расположение — на схеме листа и на листе 62; размеры — в мм по чистовым поверхностям; отметки — в м от ±0,000; высоты Н — от чистого пола помещения до оси изделия, у декора — до центра.
2. Красные цепочки — привязки электроточек и выводов: по горизонтали от угла чистовых стен, по вертикали от чистого пола, до оси изделия; звенья короче 3 мм на листе вынесены во второй ярус (ближняя к стене цепочка).
3. У знака электроточки: марка (Р — розетка, S — выключатель, Св — светильник, ЭВ — вывод кабеля), ×N — число постов в рамке, гр. — группа щита, Н — высота оси от чистого пола, мм; группы по клавишам выключателя — на листе выключателей.
4. Схема мебели, приборов и декора не является технической документацией для производства мебели; габариты — по паспортам изделий.
5. Картины и зеркала крепить к основанию по паспорту изделия (закладные и анкеры — в перечне скрытых работ); крест — ось центра предмета.
6. Двери скрытого монтажа — полотно в плоскости стены, отделка стены по полотну, плинтус прерывается у короба (узел — на листе узлов).

1000 мм · печать 1:1

| Изм. | Кол.уч | Лист | № док. | Подп. | Дата |
|---|---|---|---|---|---|
| Разраб. | | Кырлан А.С. | | | 18.10.26 |
| Пров. | | | | | |
| ГИП | | | | | |
| | | | | | |
| Н. контр. | | | | | |
| Утв. | | | | | |

**ГД-2026-008-АИ**

Квартира с кабинетом

Общая площадь 127,29* м² · * размеры со скана, не замерены (реестр — л. 6, К-1)

Дизайн-проект интерьера

| Стадия | Лист | Листов |
|---|---|---|
| РП | 81 | 92 |

**Развёртки стен. Прихожая (пом. 8)**

М 1:40

**Кырлан Александр Сергеевич**

выпуск 18.10.2026 № d2d5a25dca · стр. 92 из 129

# Развёртка стены А. Санузел гостевой (пом. 9)

Санузел гостевой (пом. 9) · вид изнутри помещения · размеры в мм, отметки в м

**ПРЕДВАРИТЕЛЬНО · не для производства работ · открыто пунктов: 4 (реестр — л. 6)**

## Развёртка стены А

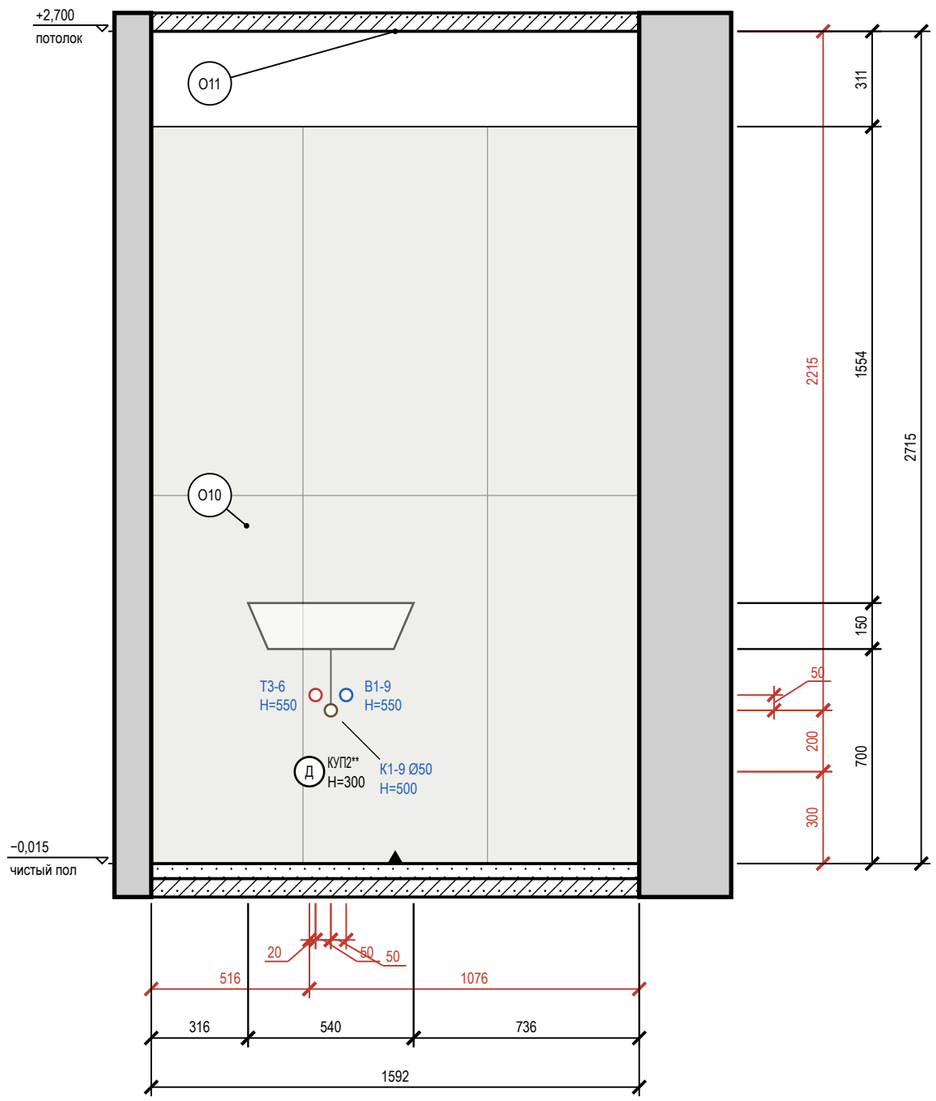


## Схема развёрток (М 1:100)

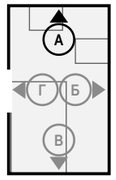


## Условные обозначения

- вывод В1 (код — в ведомости привязок)
- вывод Т3 (код — в ведомости привязок)
- вывод К1 (код — в ведомости привязок)
- привязки точек и выводов от угла и от пола, мм
- мебель и приборы — фасад по расстановке (условно)
- стены и перекрытия в сечении
- плитка: сетка швов по формату, ▲ — ось старта
- О1 — марка отделки по реестру отделки альбома
- А — марка развёртки: буква стены, стрелка — взгляд

## Ведомость отделки (на листе)

| Марка | Поверхность | Материал, изделие | Цвет, код | Кол. |
|---|---|---|---|---|
| О10 | стены | облицовка плиткой, Atlas Concorde Marvel Travertine, 600×1200×9 мм, A8UZ, затирка CG2WA | Atlas Concorde A8UZ «Marvel Travertine» | 3,8 м² |
| О11 | потолок | окраска, Tikkurila Luja 7, матовая, подготовка Q3 | Tikkurila V503 «Winter» | 4,5 м² |

**Допущения и предложения на листе**

Основа листа: размеры сняты с растрового плана заказчика с частичными размерами: рисунок не в масштабе, помещения выровнены по подписанным размерам мебели и проходов; контрольный обмер не выполнен (К-1); высота потолка 2700 мм принята: на плане заказчика её нет (К-2); толщины стен 300 / 120 мм приняты по плану заказчика, не замерены (К-1); разрешённая мощность 15 кВт принята по типовым ТУ для квартиры, ТУ заказчиком не переданы (К-4).

Знак «**» — предложение проектировщика, заказчиком не утверждено (согласовать с заказчиком): записи в реестре нет: КУП2 — по образцу: Добавлены выводы к вентиляторам: ЭВ4 (ВР1, ванная) и ЭВ5 (ВР3, санузел 2) — группа 3, высота 2389 мм, включение с основным светом, таймер выбега в вентиляторе; и коробки уравнивания потенциалов КУП1 (ванная) и КУП2 (санузел 2) — высота 300 мм, у входа, вне зон 0–2, проводник от шины PE щита ЩК, сече.

См. лист открытых вопросов (лист 6, записи К-1, К-2, К-4).

## Примечания

1. Развёртки — вид на стену изнутри помещения, по часовой стрелке; расположение — на схеме листа и на листе 62; размеры — в мм по чистовым поверхностям; отметки — в м от ±0,000; высоты Н — от чистого пола помещения до оси изделия, у декора — до центра.
2. Красные цепочки — привязки электроточек и выводов: по горизонтали от угла чистовых стен, по вертикали от чистого пола, до оси изделия; звенья короче 3 мм на листе вынесены во второй ярус (ближняя к стене цепочка).
3. У знака электроточки: марка (Р — розетка, S — выключатель, Св — светильник, ЭВ — вывод кабеля), ×N — число постов в рамке, гр. — группа щита, Н — высота оси от чистого пола, мм; группы по клавишам выключателя — на листе выключателей.
4. Схема мебели, приборов и декора не является технической документацией для производства мебели; габариты — по паспортам изделий.
5. Облицовка — по сетке швов 2 мм, раскладка от оси стены (треугольник у пола), целые ряды от пола; подрезки — по листу раскладки плитки.
6. Гидроизоляция в 2 слоя, заход на стены 200 мм — до облицовки, с актом скрытых работ и тестом проливом (узел — на листе узлов).

1000 мм · печать 1:1

| Изм. | Кол.уч | Лист | № док. | Подп. | Дата |
|---|---|---|---|---|---|
| Разраб. | | Кырлан А.С. | | | 18.10.26 |
| Пров. | | | | | |
| ГИП | | | | | |
| | | | | | |
| Н. контр. | | | | | |
| Утв. | | | | | |

**ГД-2026-008-АИ**

Квартира с кабинетом

Общая площадь 127,29* м² · * размеры со скана, не замерены (реестр — л. 6, К-1)

Дизайн-проект интерьера

| Стадия | Лист | Листов |
|---|---|---|
| РП | 82 | 92 |

**Развёртка стены А. Санузел гостевой (пом. 9)**

М 1:20

**Кырлан Александр Сергеевич**

выпуск 18.10.2026 № d2d5a25dca · стр. 93 из 129

# Развёртки стен Б, В. Санузел гостевой (пом. 9)

Санузел гостевой (пом. 9) · вид изнутри помещения · размеры в мм, отметки в м

**ПРЕДВАРИТЕЛЬНО · не для производства работ · открыто пунктов: 4 (реестр — л. 6)**

## Развёртка стены Б

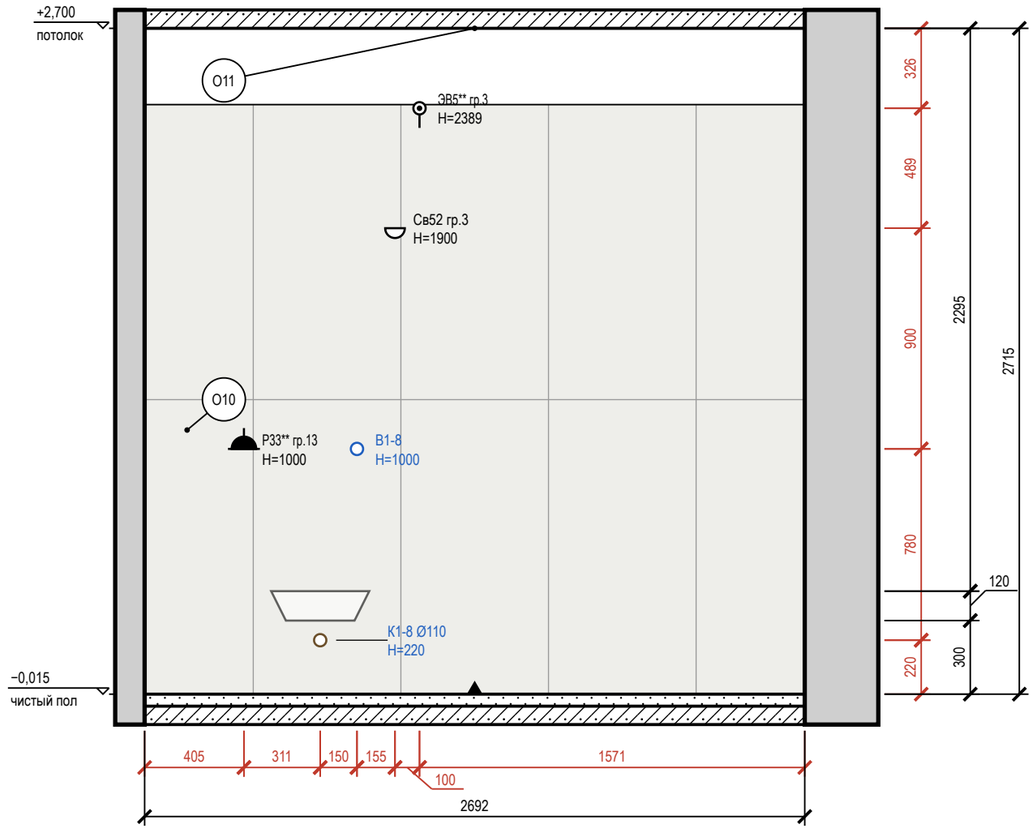


## Развёртка стены В

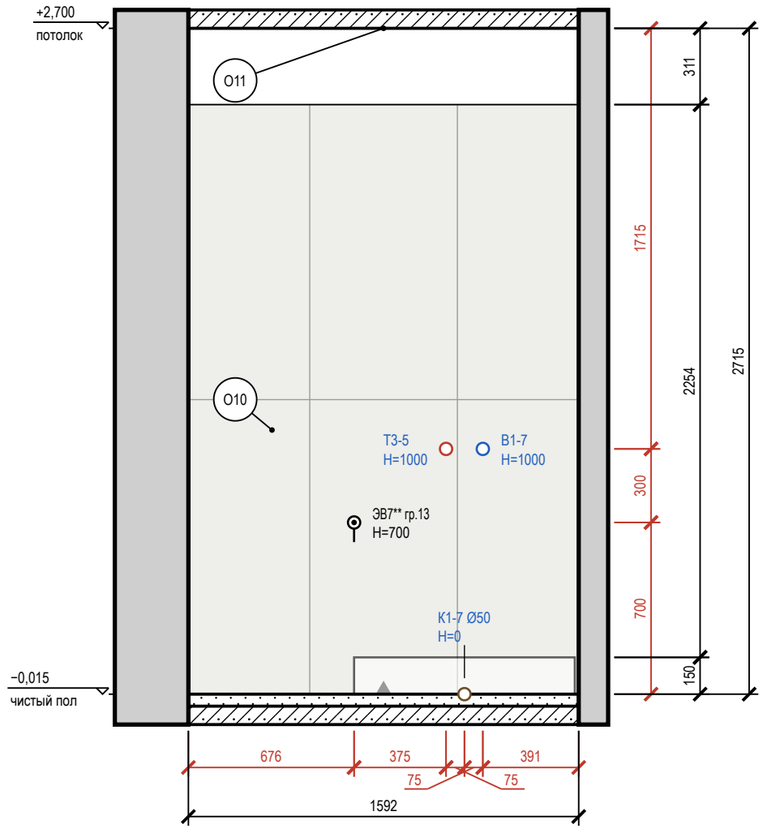


## Схема развёрток (М 1:100)

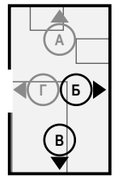


**Допущения и предложения на листе**

Основа листа: размеры сняты с растрового плана заказчика с частичными размерами: рисунок не в масштабе, помещения выровнены по подписанным размерам мебели и проходов; контрольный обмер не выполнен (К-1); высота потолка 2700 мм принята: на плане заказчика её нет (К-2); толщины стен 300 / 120 мм приняты по плану заказчика, не замерены (К-1); разрешённая мощность 15 кВт принята по типовым ТУ для квартиры, ТУ заказчиком не переданы (К-4).

Знак «**» — предложение проектировщика, заказчиком не утверждено (согласовать с заказчиком): записи в реестре нет: Р33 — по образцу: Розетка Р33 на высоте 1100 мм, вне шва плитки; ЭВ5 — по образцу: Добавлены выводы к вентиляторам: ЭВ4 (ВР1, ванная) и ЭВ5 (ВР3, санузел 2) — группа 3, высота 2389 мм, включение с основным светом, таймер выбега в вентиляторе; и коробки уравнивания потенциалов КУП1 (ванная) и КУП2 (санузел 2) — высота 300 мм, у входа, вне зон 0–2, проводник от шины PE щита ЩК, сече; ЭВ7 — по образцу: Добавлены электрические полотенцесушители IP44: П10 в ванной (480 мм, низ 900 мм) и П13 в санузле 2 (400 мм, низ 900 мм), выводы ЭВ6 и ЭВ7; мощность группы 13 — 2,4 кВт вместо 1,8 кВт.

См. лист открытых вопросов (лист 6, записи К-1, К-2, К-4).

## Условные обозначения

- розетка влагозащищённая IP44
- вывод кабеля для подключения прибора (без розетки), марка ЭВ
- светильник настенный (бра), H — высота оси
- вывод В1 (код — в ведомости привязок)
- вывод Т3 (код — в ведомости привязок)
- вывод К1 (код — в ведомости привязок)
- привязки точек и выводов от угла и от пола, мм
- мебель и приборы — фасад по расстановке (условно)
- стены и перекрытия в сечении
- плитка: сетка швов по формату, ▲ — ось старта
- О1 — марка отделки по реестру отделки альбома
- А — марка развёртки: буква стены, стрелка — взгляд

## Ведомость отделки (на листе)

| Марка | Поверхность | Материал, изделие | Цвет, код | Кол. |
|---|---|---|---|---|
| О10 | стены | облицовка плиткой, Atlas Concorde Marvel Travertine, 600×1200×9 мм, A8UZ, затирка CG2WA | Atlas Concorde A8UZ «Marvel Travertine» | 10,3 м² |
| О11 | потолок | окраска, Tikkurila Luja 7, матовая, подготовка Q3 | Tikkurila V503 «Winter» | 4,5 м² |

## Примечания

1. Развёртки — вид на стену изнутри помещения, по часовой стрелке; расположение — на схеме листа и на листе 62; размеры — в мм по чистовым поверхностям; отметки — в м от ±0,000; высоты H — от чистого пола помещения до оси изделия, у декора — до центра.
2. Красные цепочки — привязки электроточек и выводов: по горизонтали от угла чистовых стен, по вертикали от чистого пола, до оси изделия; звенья короче 3 мм на листе вынесены во второй ярус (ближняя к стене цепочка).
3. У знака электроточки: марка (Р — розетка, S — выключатель, Св — светильник, ЭВ — вывод кабеля), ×N — число постов в рамке, гр. — группа щита, H — высота оси от чистого пола, мм; группы по клавишам выключателя — на листе выключателей.
4. Схема мебели, приборов и декора не является технической документацией для производства мебели; габариты — по паспортам изделий (* — высота не задана в проекте, показана по типовому изделию).
5. Облицовка — по сетке швов 2 мм, раскладка от оси стены (треугольник у пола), целые ряды от пола; подрезки — по листу раскладки плитки.
6. Гидроизоляция в 2 слоя, заход на стены 200 мм — до облицовки, с актом скрытых работ и тестом проливом (узел — на листе узлов).

1000 мм · печать 1:1

| Изм. | Кол.уч | Лист | № док. | Подп. | Дата |
|---|---|---|---|---|---|
| Разраб. | | Кырлан А.С. | | | 18.10.26 |
| Пров. | | | | | |
| ГИП | | | | | |
| | | | | | |
| Н. контр. | | | | | |
| Утв. | | | | | |

**ГД-2026-008-АИ**

Квартира с кабинетом

Общая площадь 127,29* м² · * размеры со скана, не замерены (реестр — л. 6, К-1)

Дизайн-проект интерьера

| Стадия | Лист | Листов |
|---|---|---|
| РП | 83 | 92 |

**Развёртки стен Б, В. Санузел гостевой (пом. 9)**

М 1:25

**Кырлан Александр Сергеевич**

выпуск 18.10.2026 № d2d5a25dca · стр. 94 из 129

# Развёртка стены Г. Санузел гостевой (пом. 9)

Санузел гостевой (пом. 9) · вид изнутри помещения · размеры в мм, отметки в м

**ПРЕДВАРИТЕЛЬНО · не для производства работ · открыто пунктов: 4 (реестр — л. 6)**

## Развёртка стены Г

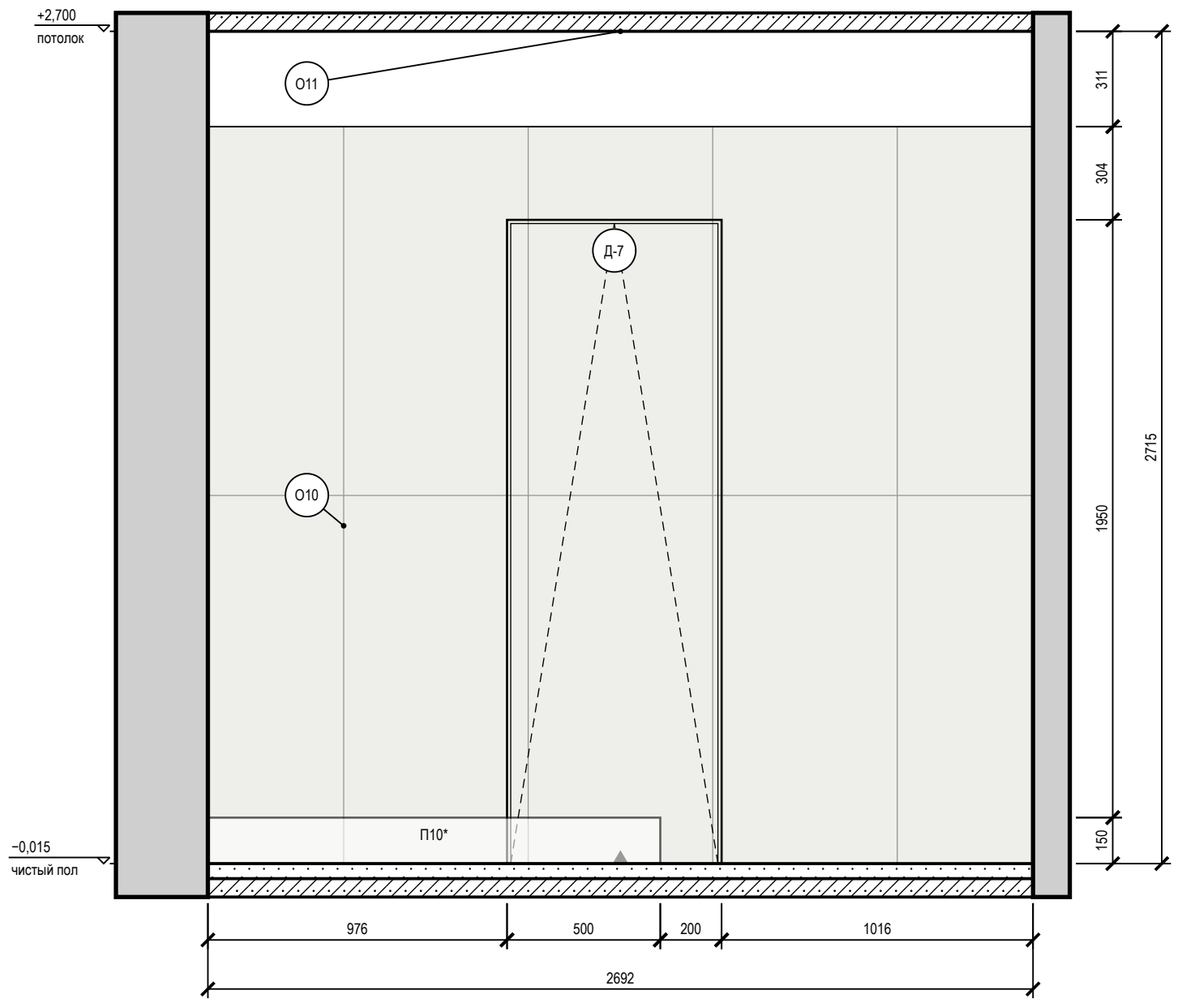


## Схема развёрток (М 1:100)

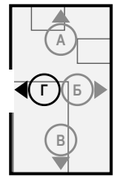


## Условные обозначения

- привязки точек и выводов от угла и от пола, мм
- мебель и приборы — фасад по расстановке (условно)
- дверь скрытого монтажа: полотно в плоскости стены (узел — на листе узлов)
- стены и перекрытия в сечении
- плитка: сетка швов по формату, ▲ — ось старта
- О1 — марка отделки по реестру отделки альбома
- А — марка развёртки: буква стены, стрелка — взгляд

## Ведомость отделки (на листе)

| Марка | Поверхность | Материал, изделие | Цвет, код | Кол. |
|---|---|---|---|---|
| О10 | стены | облицовка плиткой, Atlas Concorde Marvel Travertine, 600×1200×9 мм, A8UZ, затирка CG2WA | Atlas Concorde A8UZ «Marvel Travertine» | 5 м² |
| О11 | потолок | окраска, Tikkurila Luja 7, матовая, подготовка Q3 | Tikkurila V503 «Winter» | 4,5 м² |

**Допущения и предложения на листе**

Основа листа: размеры сняты с растрового плана заказчика с частичными размерами: рисунок не в масштабе, помещения выровнены по подписанным размерам мебели и проходов; контрольный обмер не выполнен (К-1); высота потолка 2700 мм принята: на плане заказчика её нет (К-2); толщины стен 300 / 120 мм приняты по плану заказчика, не замерены (К-1); разрешённая мощность 15 кВт принята по типовым ТУ для квартиры, ТУ заказчиком не переданы (К-4).

См. лист открытых вопросов (лист 6, записи К-1, К-2, К-4).

## Примечания

1. Развёртки — вид на стену изнутри помещения, по часовой стрелке; расположение — на схеме листа и на листе 62; размеры — в мм по чистовым поверхностям; отметки — в м от ±0,000; высоты Н — от чистого пола помещения до оси изделия, у декора — до центра.
2. Красные цепочки — привязки электроточек и выводов: по горизонтали от угла чистовых стен, по вертикали от чистого пола, до оси изделия; звенья короче 3 мм на листе вынесены во второй ярус (ближняя к стене цепочка).
3. У знака электроточки: марка (Р — розетка, S — выключатель, Св — светильник, ЭВ — вывод кабеля), ×N — число постов в рамке, гр. — группа щита, Н — высота оси от чистого пола, мм; группы по клавишам выключателя — на листе выключателей.
4. Схема мебели, приборов и декора не является технической документацией для производства мебели; габариты — по паспортам изделий (* — высота не задана в проекте, показана по типовому изделию).
5. Облицовка — по сетке швов 2 мм, раскладка от оси стены (треугольник у пола), целые ряды от пола; подрезки — по листу раскладки плитки.
6. Гидроизоляция в 2 слоя, заход на стены 200 мм — до облицовки, с актом скрытых работ и тестом проливом (узел — на листе узлов).
7. Двери скрытого монтажа — полотно в плоскости стены, отделка стены по полотну, плинтус прерывается у короба (узел — на листе узлов).

1000 мм · печать 1:1

| Изм. | Кол.уч | Лист | № док. | Подп. | Дата |
|---|---|---|---|---|---|
| Разраб. | | Кырлан А.С. | | | 18.10.26 |
| Пров. | | | | | |
| ГИП | | | | | |
| | | | | | |
| Н. контр. | | | | | |
| Утв. | | | | | |

**ГД-2026-008-АИ**

Квартира с кабинетом

Общая площадь 127,29* м² · * размеры со скана, не замерены (реестр — л. 6, К-1)

Дизайн-проект интерьера

| Стадия | Лист | Листов |
|---|---|---|
| РП | 84 | 92 |

**Развёртка стены Г. Санузел гостевой (пом. 9)**

М 1:20

**Кырлан Александр Сергеевич**

выпуск 18.10.2026 № d2d5a25dca · стр. 95 из 129

# Узлы

Пороги и стыки покрытий, скрытые двери, короба стояков, гидроизоляция, плинтус

### 1 Порог 15 мм: мокрая зона — жилое помещение (М 1:10)

Применение: двери Д-6, Д-7; места — лист 62

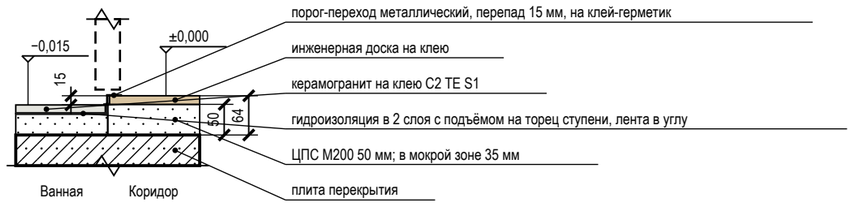


### 2 Дверь скрытого монтажа в плоскости стены, плинтус (М 1:5)

Применение: двери Д-2, Д-3, Д-4, Д-5, Д-6, Д-7; места — лист 62

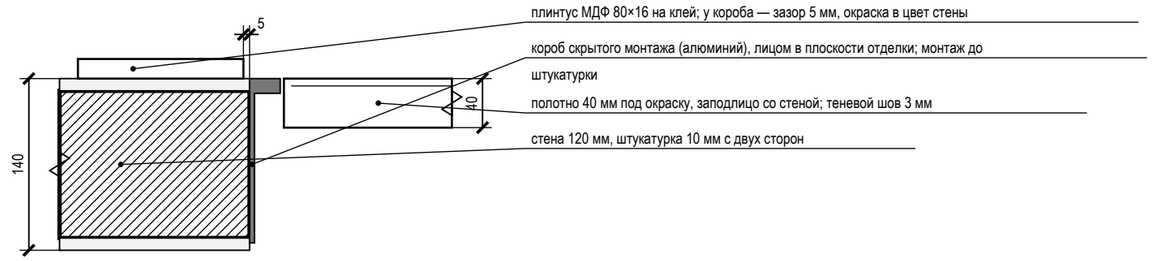


### 3 Короб стояков К1-1 с люком и звукоизоляцией (М 1:10)

Применение: пом. 9, 7, 4; места — лист 62

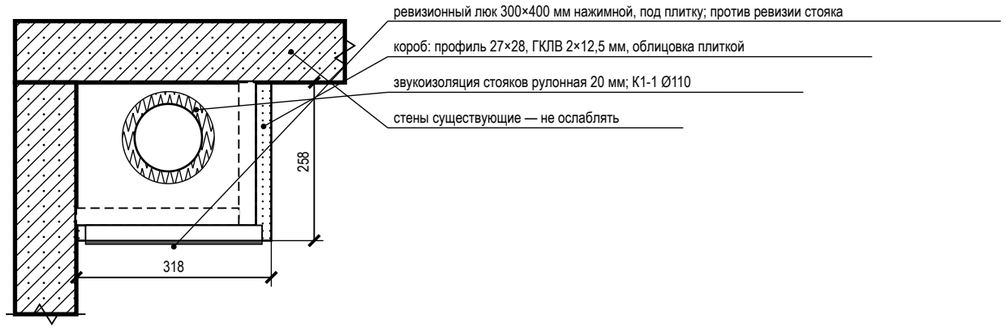


### 4 Гидроизоляция санузла: заход на стены 200 мм, примыкание ванны (М 1:20)

Применение: пом. 7, 9; места — лист 62

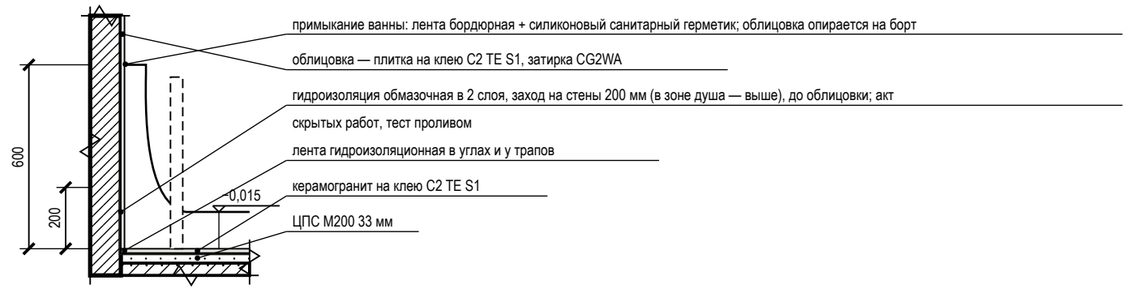


### 5 Плинтус МДФ 80×16 мм у окрашенной стены (М 1:10)

Применение: пом. 1, 2, 3, 4, 5, 6, 8; места — лист 62

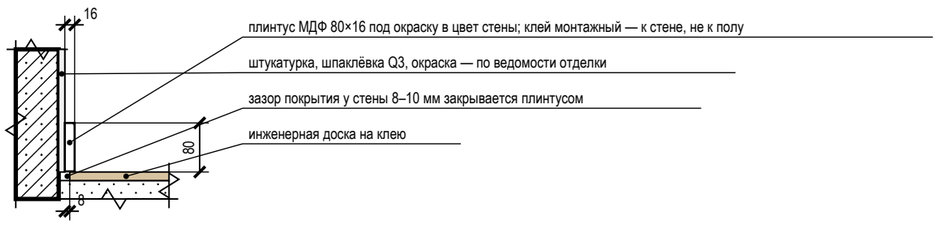


## Условные обозначения

- железобетон (плита, стены)
- кладка, перегородка
- стяжка, раствор
- гипсокартон ГКЛВ
- звукоизоляция, эластичный заполнитель
- плитка, керамогранит на клею
- инженерная доска (покрытие пола)
- металлический профиль (порог, Т-профиль, короб двери)
- гидроизоляция (обмазочная, лента)

## Примечания

1. Узлы — типовые решения проекта для мест, отмеченных выносками на листе схемы расположения развёрток и узлов; размеры — в мм, отметки — в м от ±0,000.
2. Узлы с гидроизоляцией, закладными и коробами скрытого монтажа принимаются по актам скрытых работ до закрытия отделкой; гидроизоляция — после теста проливом (24 ч).
3. Марки изделий (порог, Т-профиль, короб скрытой двери, люк) — по спецификациям; замена — на аналог с теми же габаритами по согласованию с автором проекта.

**Допущения и предложения на листе**

Основа листа: размеры сняты с растрового плана заказчика с частичными размерами: рисунок не в масштабе, помещения выровнены по подписанным размерам мебели и проходов; контрольный обмер не выполнен (К-1); высота потолка 2700 мм принята: на плане заказчика её нет (К-2); толщины стен 300 / 120 мм приняты по плану заказчика, не замерены (К-1); разрешённая мощность 15 кВт принята по типовым ТУ для квартиры, ТУ заказчиком не переданы (К-4).
См. лист открытых вопросов (лист 6, записи К-1, К-2, К-4).

| Изм. | Кол.уч | Лист | № док. | Подп. | Дата |
|---|---|---|---|---|---|
| Разраб. | | Кырлан А.С. | | | 18.10.26 |
| Пров. | | | | | |
| ГИП | | | | | |
| Н. контр. | | | | | |
| Утв. | | | | | |

**ГД-2026-008-АИ**

Квартира с кабинетом

Общая площадь 127,29* м² · * размеры со скана, не замерены (реестр — л. 6, К-1)

Дизайн-проект интерьера

| Стадия | Лист | Листов |
|---|---|---|
| РП | 85 | 92 |

**Узлы**

М б/м

**Кырлан Александр Сергеевич**

выпуск 18.10.2026 № d2d5a25dca · стр. 96 из 129

10

# Смета

Кырлан Александр Сергеевич

выпуск 18.10.2026 · d2d5a25dca · стр. 97 из 129

# Ведомость объёмов работ

Объёмы по помещениям от чертежа · площади в м², длины в м · формула, правило проёмов и источник в каждой строке

## Ведомость объёмов работ по помещениям

| Поз. | Наименование работ (материал, число слоёв) | Ед. изм. | Объём по помещениям (№ по экспликации) | | | | | | | | | Всего | Формула подсчёта | Правило проёмов | Источник | Цена за ед., ₽ | Стоимость, ₽ |
|---|---|---|---|---|---|---|---|---|---|---|---|---|---|---|---|---|---|
| | | | 1 | 2 | 3 | 4 | 5 | 6 | 7 | 8 | 9 | | | | | | |
| **1. Демонтаж и черновые работы** | | | | | | | | | | | | | | | | | |
| 1 | Демонтаж существующего покрытия пола до основания | м² | 17,89 | 5,11 | 18,92 | 45,51 | 9,07 | 9,97 | 8,44 | 7,89 | 4,49 | 127,29 | S пом. | | л. 12, 13 | по КП | |
| 2 | Демонтаж существующей отделки стен до основания | м² | 39,31 | 22,94 | 41,58 | 65,04 | 33,47 | 28,45 | 29,92 | 21,53 | 22,31 | 304,55 | P × H − проёмы | за вычетом проёмов | л. 12, 13 | по КП | |
| 3 | Демонтаж существующей отделки потолка до основания | м² | 17,89 | 5,11 | 18,92 | 45,51 | 9,07 | 9,97 | 8,44 | 7,89 | 4,49 | 127,29 | S пом. | | л. 12, 13 | по КП | |
| 4 | Демонтаж существующих дверных блоков | шт | 1 | 1 | 1 | | | 1 | 1 | 2 | | 7 | по ведомости проёмов | | л. 13, 14 | по КП | |
| 5 | Демонтаж существующих сантехприборов и электрооборудования (если есть) | компл | | | | | | | | | | | по факту на объекте | | л. 13 | по КП | |
| 6 | Устройство стяжки: стяжка ЦПС М200, 50 мм | м² | 17,94 | 5,15 | 18,97 | 45,58 | 9,39 | 10,02 | 8,49 | 8,23 | 4,53 | 128,30 | S пом. + S в дверных проёмах (b × t/2) | проёмы добавлены | л. 39–41 | 530 | 67 999 |
| 7 | Гидроизоляция обмазочная, 2 слоя: пол, стены на 200 мм, зоны замачивания | м² | | | | | | | 14,64 | | 11,02 | 25,66 | пол + (P − двери) × h заведения + зоны замачивания | | л. 35 | 450 | 11 547 |
| 8 | Штукатурка стен по маякам, до 10 мм | м² | 39,31 | 22,94 | 41,58 | 65,04 | 33,47 | 28,45 | 29,92 | 21,53 | 22,31 | 304,55 | P × H − проёмы по обводу коробок − грани перегородок на ГКЛВ | за вычетом проёмов | л. 12, 40, 41 | 530 | 161 412 |
| 9 | Штукатурка оконных откосов шириной более 200 мм | м² | 2,16 | | 2,07 | 2,94 | | 2,09 | | | | 9,26 | Σ (2h + b) × глубина откоса | откосы > 200 мм | л. 12 | 540 | 5 000 |
| **Итого по разделу 1 — 245 958 ₽ (позиций 9, из них по КП 5); в сводную смету — л. 91, 92** | | | | | | | | | | | | | | | | | |
| **2. Инженерные системы** | | | | | | | | | | | | | | | | | |
| 10 | Прокладка слаботочной линии: Кабель домофона — тип по системе поставщика, отдельно от силовых | м | | | | | | | | | | 5,70 | по лучам от ЩС**: 1 точ., запас 10 % | | л. 27 | по КП | |
| 11 | Прокладка слаботочной линии: Кабель коаксиальный RG-6 (75 Ом) к розеткам ТВ, отдельно от силовых | м | | | | | | | | | | 52,50 | по лучам от ЩС**: 3 точ., запас 10 % | | л. 27 | по КП | |
| 12 | Прокладка слаботочной линии: Кабель U/UTP кат. 6 (LAN, Wi-Fi и камеры по PoE), отдельно от силовых | м | | | | | | | | | | 97,00 | по лучам от ЩС**: 6 точ., запас 10 % | | л. 27 | по КП | |
| 13 | Прокладка гофротрубы Ø20 для слаботочных линий, отдельно от силовых | м | | | | | | | | | | 139,70 | по длине лучей без участков в канале плинтуса (≈ 90 %) | | л. 27 | по КП | |
| 14 | Сборка слаботочного щита ЩС**: корпус, патч-панель, подключение линий и питания 220 В; коммутатор и точки доступа — оборудование заказчика | шт | | | | | | | | | | 1 | один щит | | л. 23, 24, 27 | по КП | |
| 15 | Электроточка: подрозетник в бетоне, розетка, выключатель, вывод | шт | 10 | | 11 | 20 | 4 | 11 | 4 | 8 | 3 | 71 | по ведомости электроточек | | л. 20, 23, 24 | 950 | 67 450 |
| 16 | Штробы в стенах под спуски кабеля к точкам — выполняются только после технического заключения о несущих стенах | м | 19,20 | | 21,80 | 26,85 | 7,80 | 21,80 | 5,67 | 12,40 | 4,06 | 119,58 | Σ (H − h) по точкам на стенах: вертикальные спуски | после техзаключения | л. 13, 20 | по КП | |
| 17 | Установка встраиваемого точечного светильника | шт | 8 | | 6 | 14 | 2 | 6 | 3 | 4 | 2 | 45 | по плану освещения | | л. 21 | 750 | 33 750 |
| 18 | Монтаж светильника: потолочного, подвесного, настенного | шт | 2 | 1 | 2 | 3 | | 2 | 1 | | 1 | 12 | по плану освещения | | л. 21 | 1 200 | 14 400 |
| 19 | Монтаж LED-ленты в алюминиевый профиль | м | 15,50 | | 12,30 | 25,10 | | 12,30 | | 1,80 | | 67,00 | Σ длин лент по плану освещения | | л. 21 | 230 | 15 410 |
| 20 | Установка блока питания LED в доступном месте (люк, шкаф) | шт | 1 | | 1 | 2 | | 1 | | 1 | | 6 | один на LED-группу | | л. 21 | 570 | 3 420 |
| 21 | Установка автономного пожарного извещателя | шт | 1 | | 1 | 2 | 1 | 1 | | 1 | | 7 | по плану розеток | | л. 20 | по КП | |
| 22 | Сборка щита: установка автоматов и АВДТ групп, вводного автомата | шт | | | | | | | | | | 6 | группы + вводной автомат | | л. 25 | 230 | 1 380 |
| 23 | Установка вводного УЗО | шт | | | | | | | | | | 1 | по однолинейной схеме | | л. 25 | 380 | 380 |

**Допущения и предложения на листе**

Основа листа: размеры сняты с растрового плана заказчика с частичными размерами: рисунок не в масштабе, помещения выровнены по подписанным размерам мебели и проходов; контрольный обмер не выполнен (К-1); высота потолка 2700 мм принята: на плане заказчика её нет (К-2); толщины стен 300 / 120 мм приняты по плану заказчика, не замерены (К-1); разрешённая мощность 15 кВт принята по типовым ТУ для квартиры, ТУ заказчиком не переданы (К-4).

Знак «**» — предложение проектировщика, заказчиком не утверждено (согласовать с заказчиком): записи в реестре нет: ЩС — щит слаботочный: место и состав.

См. лист открытых вопросов (лист 6, записи К-1, К-2, К-4).

| Изм. | Кол.уч | Лист | № док. | Подп. | Дата |
|---|---|---|---|---|---|
| Разраб. | | Кырлан А.С. | | | 18.10.26 |
| Пров. | | | | | |
| ГИП | | | | | |
| | | | | | |
| Н. контр. | | | | | |
| Утв. | | | | | |

**ГД-2026-008-АИ**

Квартира с кабинетом

Общая площадь 127,29* м² · * размеры со скана, не замерены (реестр — л. 6, К-1)

Дизайн-проект интерьера

| Стадия | Лист | Листов |
|---|---|---|
| РП | 86 | 92 |

**Ведомость объёмов работ**

М б/м

**Кырлан Александр Сергеевич**

# Ведомость объёмов работ (продолжение)

Объёмы по помещениям от чертежа · площади в м², длины в м · формула, правило проёмов и источник в каждой строке

## Ведомость объёмов работ по помещениям (продолжение)

| Поз. | Наименование работ (материал, число слоёв) | Ед. изм. | Объём по помещениям (№ по экспликации) | | | | | | | | | Всего | Формула подсчёта | Правило проёмов | Источник | Цена за ед., ₽ | Стоимость, ₽ |
|---|---|---|---|---|---|---|---|---|---|---|---|---|---|---|---|---|---|
| | | | 1 | 2 | 3 | 4 | 5 | 6 | 7 | 8 | 9 | | | | | | |
| 24 | Монтаж инсталляции, установка подвесного унитаза и кнопки смыва | шт | | | | | | | 1 | | 1 | 2 | по плану выводов | | л. 30, 32 | 10 500 | 21 000 |
| 25 | Короб инсталляции: каркас и обшивка ГКЛВ в 2 слоя, ревизионный доступ к смыву | шт | | | | | | | 1 | | 1 | 2 | по плану выводов | | л. 30, 35–38 | по КП | |
| 26 | Короб К1 над чистым полом: каркас и обшивка ГКЛВ под плитку (материалы — в спецификации ВК) | м.п. | | | | | | | 9,88 | | 3,90 | 13,78 | Σ открытых участков выпусков К1 (профиль листа разводки ВК) | | л. 30, 32 | по КП | |
| 27 | Установка ванны с сифоном | шт | | | | | | | 1 | | | 1 | по плану выводов | | л. 30, 32 | 6 000 | 6 000 |
| 28 | Установка умывальника (мойки) с сифоном и смесителем | шт | | | | | | | 2 | | 1 | 3 | по плану выводов | | л. 30, 32 | 3 000 | 9 000 |
| 29 | Установка душевого поддона с трапом, ограждения | шт | | | | | | | | | 1 | 1 | по плану выводов | | л. 30, 32 | по КП | |
| 30 | Подключение стиральной (посудомоечной) машины к ВК | шт | | | | | | | 1 | | | 1 | по плану выводов | | л. 30 | по КП | |
| 31 | Установка радиатора с узлом подключения и терморегулятором | шт | 2 | | 2 | 3 | | 2 | | | | 9 | по плану отопления | | л. 29 | по КП | |
| **Итого по разделу 2 — 172 190 ₽ (позиций 22, из них по КП 12); в сводную смету — л. 91, 92** | | | | | | | | | | | | | | | | | |
| **3. Чистовые работы** | | | | | | | | | | | | | | | | | |
| 32 | Облицовка стен керамогранитом 600×1200 на клею | м² | | | | | | | 25,34 | | 18,87 | 44,21 | по раскладке: зона облицовки − место за коробом | за вычетом проёмов | л. 35–38 | 2 500 | 110 525 |
| 33 | Облицовка короба инсталляции (ГКЛВ) керамогранитом: лицо, боковины, полка | м² | | | | | | | 1,76 | | 1,47 | 3,23 | по раскладке: лицо, боковины, полка | | л. 35–38 | 2 500 | 8 075 |
| 34 | Облицовка фартука керамогранитом 1200×600 | м² | | | | 0,70 | | | | | | 0,70 | по раскладке фартука | | л. 35–38, 40, 41 | 2 400 | 1 680 |
| 35 | Укладка керамогранита на пол, 600×1200, на клею | м² | | | | | | | 8,49 | 8,23 | 4,53 | 21,25 | S пом. + S в дверных проёмах | проёмы добавлены | л. 35–39 | 1 800 | 38 250 |
| 36 | Затирка швов керамогранита | м² | | | | 0,70 | | | 35,54 | 7,89 | 24,83 | 68,96 | Σ S облицовки и пола из плитки | | л. 35–38 | 150 | 10 344 |
| 37 | Грунтование стен, 2 слоя (под штукатурку и под отделку) | м² | 39,31 | 22,94 | 41,58 | 65,04 | 33,47 | 28,45 | 29,92 | 21,53 | 22,31 | 304,55 | P × H − проёмы | за вычетом проёмов | л. 40, 41 | 96 | 29 237 |
| 38 | Шпаклёвка стен под окраску, 2 слоя (старт и финиш), уровень Q3 | м² | 39,31 | 22,94 | 41,58 | 64,34 | 33,47 | 28,45 | | 21,53 | | 251,62 | P × H − проёмы − фартук | за вычетом проёмов | л. 40, 41 | 750 | 188 715 |
| 39 | Грунтование и шпаклёвка оконных откосов, 2 слоя | м.п. | 9,40 | | 9,00 | 12,80 | | 9,10 | | | | 40,30 | Σ (2h + b) по окнам | по окнам | л. 12 | 300 | 12 090 |
| 40 | Грунтование потолка, 2 слоя | м² | 17,89 | 5,11 | 18,92 | 45,51 | 9,07 | 9,97 | 8,44 | 7,89 | 4,49 | 127,29 | S пом. | | л. 40, 41 | 96 | 12 220 |
| 41 | Шпаклёвка потолка под окраску, 2 слоя, уровень Q3 | м² | 17,89 | 5,11 | 18,92 | 45,51 | 9,07 | 9,97 | 8,44 | 7,89 | 4,49 | 127,29 | S пом. | | л. 34, 40, 41 | 950 | 120 926 |
| 42 | Окраска потолка водно-дисперсионной краской, 2 слоя | м² | 17,89 | 5,11 | 18,92 | 45,51 | 9,07 | 9,97 | 8,44 | 7,89 | 4,49 | 127,29 | S пом. | | л. 40, 41 | 360 | 45 824 |
| 43 | Окраска стен водно-дисперсионной краской, 2 слоя | м² | 45,79 | 24,41 | 47,63 | 72,42 | 44,60 | 34,45 | | 30,35 | | 299,65 | P × H − фартук, проёмы не вычитаются | без вычета проёмов | л. 40, 41 | 300 | 89 895 |
| 44 | Окраска оконных откосов, 2 слоя | м.п. | 9,40 | | 9,00 | 12,80 | | 9,10 | | | | 40,30 | Σ (2h + b) по окнам | по окнам | л. 12 | 120 | 4 836 |
| 45 | Укладка инженерной доски на клей | м² | 17,94 | 5,15 | 18,97 | 45,58 | 9,39 | 10,02 | | | | 107,05 | S пом. + S в дверных проёмах | проёмы добавлены | л. 39–41 | 1 200 | 128 460 |
| 46 | Установка плинтуса МДФ h=80 мм | м.п. | 16,16 | 8,34 | 16,74 | 25,88 | 11,22 | 11,96 | | 7,04 | | 97,34 | P − ширина дверных проёмов | | л. 40, 41 | 450 | 43 803 |
| 47 | Окраска плинтуса в тоне No. 15, 2 слоя | м.п. | 16,16 | 8,34 | 16,74 | 25,88 | 11,22 | 11,96 | | 7,04 | | 97,34 | как плинтус | | л. 40, 41 | 300 | 29 202 |
| 48 | Монтаж дверей скрытого монтажа под покраску (поставщик дверей) | шт | 1 | 1 | 1 | | | 1 | 1 | 1 | | 6 | по ведомости проёмов | | л. 14 | 5 250 | 31 500 |
| 49 | Входная дверь, поставка с монтажом и откосами | шт | | | | | | | | | | 1 | по ведомости проёмов | | л. 14 | по КП | |
| **Итого по разделу 3 — 905 582 ₽ (позиций 18, из них по КП 1); в сводную смету — л. 91, 92** | | | | | | | | | | | | | | | | | |

**Допущения и предложения на листе**

Основа листа: размеры сняты с растрового плана заказчика с частичными размерами: рисунок не в масштабе, помещения выровнены по подписанным размерам мебели и проходов; контрольный обмер не выполнен (К-1); высота потолка 2700 мм принята: на плане заказчика её нет (К-2); толщины стен 300 / 120 мм приняты по плану заказчика, не замерены (К-1); разрешённая мощность 15 кВт принята по типовым ТУ для квартиры, ТУ заказчиком не переданы (К-4).

См. лист открытых вопросов (лист 6, записи К-1, К-2, К-4).

| Изм. | Кол.уч | Лист | № док. | Подп. | Дата |
|---|---|---|---|---|---|
| Разраб. | | Кырлан А.С. | | | 18.10.26 |
| Пров. | | | | | |
| ГИП | | | | | |
| | | | | | |
| Н. контр. | | | | | |
| Утв. | | | | | |

**ГД-2026-008-АИ**

Квартира с кабинетом

Общая площадь 127,29* м² · * размеры со скана, не замерены (реестр — л. 6, К-1)

Дизайн-проект интерьера

| Стадия | Лист | Листов |
|---|---|---|
| РП | 87 | 92 |

**Ведомость объёмов работ (продолжение)**

М б/м

**Кырлан Александр Сергеевич**

# Ведомость объёмов работ (окончание)

**ПРЕДВАРИТЕЛЬНО · не для производства работ · открыто пунктов: 4 (реестр — л. 6)**

Объёмы по помещениям от чертежа · площади в м², длины в м · формула, правило проёмов и источник в каждой строке

## Ведомость подсчёта площадей по помещениям

| № | Помещение | S пола, м² | P, м | H, м | P × H, м² | Проёмы, м² | Стены нетто, м² | В дверных проёмах, м² | Плинтус, м | Откосы, м.п. |
|---|---|---|---|---|---|---|---|---|---|---|
| 1 | Спальня | 17,89 | 16,96 | 2,70 | 45,79 | 6,48 | 39,31 | 0,05 | 16,16 | 9,40 |
| 2 | Гардеробная-постирочная | 5,11 | 9,04 | 2,70 | 24,41 | 1,47 | 22,94 | 0,04 | 8,34 | нет |
| 3 | Кабинет | 18,92 | 17,64 | 2,70 | 47,63 | 6,05 | 41,58 | 0,05 | 16,74 | 9,00 |
| 4 | Кухня-гостиная | 45,51 | 27,08 | 2,70 | 73,12 | 8,08 | 65,04 | 0,07 | 25,88 | 12,80 |
| 5 | Коридор | 9,07 | 16,52 | 2,70 | 44,60 | 11,13 | 33,47 | 0,32 | 11,22 | нет |
| 6 | Детская | 9,97 | 12,76 | 2,70 | 34,45 | 6,00 | 28,45 | 0,05 | 11,96 | 9,10 |
| 7 | Ванная | 8,44 | 11,64 | 2,71 | 31,60 | 1,68 | 29,92 | 0,05 | нет | нет |
| 8 | Прихожая | 7,89 | 11,24 | 2,70 | 30,35 | 8,82 | 21,53 | 0,34 | 7,04 | нет |
| 9 | Санузел гостевой | 4,49 | 8,76 | 2,71 | 23,78 | 1,47 | 22,31 | 0,04 | нет | нет |
| | **Итого** | **127,29** | | | **355,73** | **51,18** | **304,55** | **1,01** | **97,34** | **40,30** |

## Реестр контрольных сумм

| Показатель | По ВОР | По чертежу | Расхождение | Лист |
|---|---|---|---|---|
| Σ площадей помещений без летних, м² — общая площадь по экспликации | 127,29 | 127,29 | 0,0 % | л. 12 |
| Стены под окраску, м² (шпаклёвка) ведомость отделки | 251,62 | 251,62 | 0,0 % | л. 40, 41 |
| Потолки под окраску, м² — ведомость отделки | 127,29 | 127,29 | 0,0 % | л. 40, 41 |
| Плинтус, м — ведомость отделки | 97,34 | 97,34 | 0,0 % | л. 40, 41 |
| Плитка к заказу, шт — ведомость плитки | 166 | 166 | 0,0 % | л. 35 |
| Гидроизоляция, м² — ведомость материалов плитки | 25,66 | 25,66 | 0,0 % | л. 35 |
| Точки ЭОМ, шт — планы ЭОМ (без щитов) | 147 | 149 | -1,3 % | л. 20, 21 |

## Примечания

1. Объёмы — от геометрии проекта (та же, что на планах и в ведомости отделки), не от общей площади: P — периметр чистого контура, H — от чистого пола до низа потолка, проёмы — по наружному обводу коробок.
2. Подсчёт по ГЭСН-2001-15 и ГЭСН-2001-11: штукатурка и шпаклёвка стен — за вычетом проёмов; окраска водными составами — без вычета проёмов (п. 2.24); откосы — отдельно, по ширине до 200 и более 200 мм; полы — с площадью в дверных проёмах.
3. Плитка — по раскладке (целые и с подрезкой); короб инсталляции и фартук — отдельными строками, двойного счёта облицовки нет. Материалы, запас и количество к заказу — в спецификации материалов.
4. Цены — ориентир по открытым прайсам Москвы (цены на 21.09.2026), не коммерческое предложение; «по КП» — расценки нет, строка в итог не входит.
5. Демонтаж — по плану демонтажа и общим указаниям: покрытия пола, отделка стен и потолков, дверные блоки — до основания; объёмы справочные, уточняются по факту на объекте (расценки в книге нет — «по КП»).
6. Штробы в стенах — только после технического заключения о несущих стенах (общие указания, план обмера и демонтажа): строка «Штробы в стенах» вертикальные спуски кабеля от потолочной трассы к точкам, объём не меньше фактического (горизонтальные трассы — по исполнительной схеме). Расценки штробления в прайсе нет — «по КП», в итог не входит; кабель в штробах стен прокладывается после неё.
7. Площадь облицовки стен — одно число с тремя названиями: зона облицовки по ведомости отделки 45,89 м² − место за коробом инсталляции 1,68 м² (плитку туда не кладут) = стены под плитку 44,21 м² (строка «Облицовка стен»); облицовка коробов 3,23 м² — отдельной строкой; стены и короба вместе — 47,44 м² (столько плитки по раскладке в спецификации). Источник — один (quantities.js), расхождение на листах ловит.
8. Слаботочные сети: кабель по лучам от ЩС** 155,20 м (U/UTP, RG-6, домофон — по видам), гофра 139,70 м, щит ЩС** с патч-панелью; розетки RJ45 и ТВ монтируются в строке «Электроточка». Длины те же, что в ведомости изделий электрика (одна модель — lowcurrent-engineer/bom.js); оборудование заказчика (точки доступа, камеры, коммутатор) в спецификацию не входит. 2 точ. — предложение листа слаботочки.
9. Коробы: стояков (нет) и К1 над чистым полом (13,78 м открытых участков; труба К1 вдоль стен 33,68 м в короб не зашивается — она за приборами, в раме инсталляции и в шахтах). В спецификации ВК короб К1 заказывается с запасом 10 % — 15,20 м. Материалы коробов стояков и инсталляции — в спецификации материалов, К1 — в спецификации ВК.

**Допущения и предложения на листе**

Основа листа: размеры сняты с растрового плана заказчика с частичными размерами: рисунок не в масштабе, помещения выровнены по подписанным размерам мебели и проходов; контрольный обмер не выполнен (К-1); высота потолка 2700 мм принята: на плане заказчика её нет (К-2); толщины стен 300 / 120 мм приняты по плану заказчика, не замерены (К-1); разрешённая мощность 15 кВт принята по типовым ТУ для квартиры, ТУ заказчиком не переданы (К-4).

Знак «**» — предложение проектировщика, заказчиком не утверждено (согласовать с заказчиком): записи в реестре нет: ЩС — щит слаботочный: место и состав.

См. лист открытых вопросов (лист 6, записи К-1, К-2, К-4).

| Изм. | Кол.уч | Лист | № док. | Подп. | Дата |
|---|---|---|---|---|---|
| Разраб. | | Кырлан А.С. | | | 18.10.26 |
| Пров. | | | | | |
| ГИП | | | | | |
| | | | | | |
| Н. контр. | | | | | |
| Утв. | | | | | |

**ГД-2026-008-АИ**

Квартира с кабинетом

Общая площадь 127,29* м² · * размеры со скана, не замерены (реестр — л. 6, К-1)

Дизайн-проект интерьера

| Стадия | Лист | Листов |
|---|---|---|
| РП | 88 | 92 |

**Ведомость объёмов работ (окончание)**

М б/м

**Кырлан Александр Сергеевич**

выпуск 18.10.2026 № d2d5a25dca · стр. 100 из 129

# Спецификация материалов

Отделочные материалы: чистое количество, запас, упаковка, к заказу · ГОСТ 21.110-2013

**ПРЕДВАРИТЕЛЬНО · не для производства работ · открыто пунктов: 4 (реестр — л. 6)**

## Спецификация материалов (ГОСТ 21.110-2013, форма 1)

| Поз. | Наименование и техническая характеристика | Тип, марка, артикул | Код продукции | Поставщик | Ед. изм. | Количество | | | | Масса ед., кг | Примечание |
|---|---|---|---|---|---|---|---|---|---|---|---|
| | | | | | | чистое | запас, % | упаковка | к заказу | | |
| **Покрытия полов и облицовка** | | | | | | | | | | | |
| 1 | Инженерная доска (дуб натуральный, рабочий слой 4 мм, эмиссия E1, прямая укладка) | 1167-4250 | | | м² | 107,05 | 7 | по артикулу | 114,60 м² | | пом. 1, 2, 3, 4, 5, 6; до целой упаковки; л. 39–41 |
| 2 | Клей для паркетной и инженерной доски (эластичный, по ТУ изготовителя доски) | по выбору подрядчика | | | м² | 107,05 | | ведро по ТУ | по ТУ | | расход кг/м² — по ТУ клея; л. 39 |
| 3 | Керамогранит 600×600 мм под травертин | аналог: керамогранит под травертин | | | шт | 45 | 10 | коробка | 50 шт | | 13 целых + 32 с подрезкой; 12,93 м² по раскладке, к заказу 18,00 м²; пом. 7, 9; л. 35–38 |
| 4 | Керамогранит 600×1200 мм под травертин | аналог: керамогранит под травертин | | | шт | 84 | 10 | коробка | 96 шт | | 34 целых + 50 с подрезкой; 47,44 м² по раскладке, к заказу 69,12 м²; пом. 7, 9; л. 35–38 |
| 5 | Керамогранит 600×1200 мм A8UZ | A8UZ | | | шт | 15 | 10 | коробка | 17 шт | | 3 целых + 12 с подрезкой; 7,89 м² по раскладке, к заказу 12,24 м²; пом. 8; л. 35–38 |
| 6 | Керамогранит 1200×600 мм под травертин, матовый | аналог: керамогранит под травертин, матовый | | | шт | 2 | 10 | коробка | 3 шт | | 0 целых + 2 с подрезкой; 0,70 м² по раскладке, к заказу 2,16 м²; пом. 4; л. 35–38 |
| **Сухие смеси и гидроизоляция** | | | | | | | | | | | |
| 7 | Клей плиточный цементный класса C2 TE S1 (ГОСТ Р 56387-2018) | Ceresit CM 17 или аналог | | | кг | 492,84 | 10 | мешок 25 кг | 22 меш. | 25 | слой 5 мм, 1,50 кг/м² на 1 мм; л. 35 |
| 8 | Затирка цементная класса CG2WA, цвет — по колерной карте | Mapei Ultracolor Plus 132 или аналог | | | кг | 4,99 | 10 | упак. 2 кг | 3 упак. | 2 | расход (a+b)/ab × шов × t × 1,6 кг/м²; л. 35 |
| 9 | Гидроизоляция обмазочная полимерная, 2 слоя, лента в углах, манжеты на выводах | по выбору подрядчика | | | м² | 25,66 | 10 | ведро по ТУ | по ТУ | | пом. 7, 9; расход кг/м² — по ТУ; л. 35 |
| 10 | Лента демпферная по периметру пола из плитки | по выбору подрядчика | | | м | 25,44 | 10 | рулон | 28,00 м | | л. 35 |
| 11 | Смесь цементно-песчаная для стяжки М200 (50 мм, 33 мм) | по выбору подрядчика | | | м³ | 6,19 | 5 | мешок по ТУ | по ТУ | | S 128,30 м² × толщина; армирование и маяки — по ТУ; л. 39 |
| 12 | Смесь штукатурная гипсовая для машинного и ручного нанесения по маякам, слой до 10 мм | по выбору подрядчика | | | м² | 304,55 | 10 | мешок по ТУ | по ТУ | | пом. 1, 2, 3, 4, 5, 6, 7, 8, 9; расход кг/м² на 1 мм слоя — по ТУ смеси, толщина — по замеру кривизны стен; л. 12, 40, 41 |
| **Короба из ГКЛВ** | | | | | | | | | | | |
| 13 | Лист ГКЛВ 12,5 мм, 2500 × 1200 мм, обшивка коробов в 2 слоя | по выбору подрядчика | | | м² | 6,46 | 10 | лист 3,00 м² | 3,00 лист | | инсталляция пом. 7: 1,76 м²; инсталляция пом. 9: 1,47 м²; площадь × 2 слоя; короб К1 над полом — в спецификации ВК; л. 30, 35–38 |
| 14 | Профиль стальной оцинкованный 27 × 28 мм: каркас коробов (стойки и направляющие) | по выбору подрядчика | | | м | 15,60 | 10 | хлыст 3 м | 6 шт | | стойки через 400 мм по свободному периметру + направляющие по полу и потолку; крепёж, лента, шпаклёвка швов — по узлу короба; л. 30, 35–38 |
| **Слаботочные сети** | | | | | | | | | | | |
| 15 | Кабель домофона — тип по системе поставщика | по выбору подрядчика | | | м | 5,70 | | бухта по ТУ | 6,00 м | | по лучам от ЩС**, 1 точ., запас 10 % уже в длине; 2 точ. — предложение листа слаботочки (знак «*» на плане); л. 27 |
| 16 | Кабель коаксиальный RG-6 (75 Ом) к розеткам ТВ | по выбору подрядчика | | | м | 52,50 | | бухта по ТУ | 53,00 м | | по лучам от ЩС**, 3 точ., запас 10 % уже в длине; 2 точ. — предложение листа слаботочки (знак «*» на плане); л. 27 |
| 17 | Кабель U/UTP кат. 6 (LAN, Wi-Fi и камеры по PoE) | по выбору подрядчика | | | м | 97,00 | | бухта по ТУ | 97,00 м | | по лучам от ЩС**, 6 точ., запас 10 % уже в длине; 2 точ. — предложение листа слаботочки (знак «*» на плане); л. 27 |

**Допущения и предложения на листе**

Основа листа: размеры сняты с растрового плана заказчика с частичными размерами: рисунок не в масштабе, помещения выровнены по подписанным размерам мебели и проходов; контрольный обмер не выполнен (К-1); высота потолка 2700 мм принята: на плане заказчика её нет (К-2); толщины стен 300 / 120 мм приняты по плану заказчика, не замерены (К-1); разрешённая мощность 15 кВт принята по типовым ТУ для квартиры, ТУ заказчиком не переданы (К-4).

Знак «**» — предложение проектировщика, заказчиком не утверждено (согласовать с заказчиком): записи в реестре нет: ЩС — щит слаботочный: место и состав; плинтус пом. 1–5, 8, фартук пом. 4 — артикул изделия не выбран: позиция описана характеристиками («аналог по характеристикам»), артикул выбирается при закупке.

См. лист открытых вопросов (лист 6, записи К-1, К-2, К-4).

| Изм. | Кол.уч | Лист | № док. | Подп. | Дата |
|---|---|---|---|---|---|
| Разраб. | | Кырлан А.С. | | | 18.10.26 |
| Пров. | | | | | |
| ГИП | | | | | |
| | | | | | |
| Н. контр. | | | | | |
| Утв. | | | | | |

**ГД-2026-008-АИ**

Квартира с кабинетом

Общая площадь 127,29* м² · * размеры со скана, не замерены (реестр — л. 6, К-1)

Дизайн-проект интерьера

| Стадия | Лист | Листов |
|---|---|---|
| РП | 89 | 92 |

**Спецификация материалов**

М б/м

**Кырлан Александр Сергеевич**

# Спецификация материалов (окончание)

Отделочные материалы: чистое количество, запас, упаковка, к заказу · ГОСТ 21.110-2013

## Спецификация материалов (ГОСТ 21.110-2013, форма 1) (продолжение)

| Поз. | Наименование и техническая характеристика | Тип, марка, артикул | Код продукции | Поставщик | Ед. изм. | Количество | | | | Масса ед., кг | Примечание |
|---|---|---|---|---|---|---|---|---|---|---|---|
| | | | | | | чистое | запас, % | упаковка | к заказу | | |
| 18 | Гофротруба Ø20 для слаботочных линий, отдельно от силовых | по выбору подрядчика | | | м | 139,70 | | бухта по ТУ | 140,00 м | | по длине лучей без участков в канале плинтуса (≈ 90 %); л. 27 |
| 19 | Розетка компьютерная RJ45, кат. 6, с рамкой и подрозетником | по выбору подрядчика | | | шт | 4 | | шт | 4 шт | | LAN1–LAN3; серия механизмов — как у розеток и выключателей; л. 23, 24, 27 |
| 20 | Розетка телевизионная (коаксиальная) с рамкой и подрозетником | по выбору подрядчика | | | шт | 3 | | шт | 3 шт | | ТВ1, ТВ2; серия механизмов — как у розеток и выключателей; л. 23, 24, 27 |
| 21 | Трубка или монитор домофона (поставка домофонной организации) | по выбору подрядчика | | | шт | 1 | | шт | 1 шт | | ДФ1; серия механизмов — как у розеток и выключателей; л. 23, 24, 27 |
| 22 | Щит слаботочный ЩС**: корпус, DIN-рейка, розетки 220 В | по выбору подрядчика | | | шт | 1 | | шт | 1 шт | | ЩС**; серия механизмов — как у розеток и выключателей; л. 23, 24, 27 |
| 23 | Патч-панель, портов не менее 6 | по выбору подрядчика | | | шт | 1 | | шт | 1 шт | | серия механизмов — как у розеток и выключателей; л. 23, 24, 27 |
| **Лакокрасочные материалы** | | | | | | | | | | | |
| 24 | Краска интерьерная акриловая, матовая, класс истирания 1 | Farrow & Ball Modern Emulsion No. 34 «Calke Green — традиционный шалфей» | | | л | 8,88 | 10 | банка 2,5 л | 4 банк | | 37,02 м² × 2 сл. × 0,12 л/м²; пом. 1, 3, 4, 6; л. 40, 41 |
| 25 | Краска интерьерная акриловая, матовая, класс истирания 1 | Farrow & Ball Modern Emulsion No. 15 «Bone мягкий каменно-серый с зеленцой» | | | л | 46,00 | 10 | банка 2,5 л | 21 банк | | 191,66 м² × 2 сл. × 0,12 л/м²; пом. 1, 3, 4, 5, 6, 8; л. 40, 41 |
| 26 | Краска интерьерная акриловая, глубокоматовая, класс истирания 2 | Tikkurila Anti-Reflex 2 V503 «Winter» | | | л | 27,45 | 10 | банка 2,7 л | 12 банк | | 114,36 м² × 2 сл. × 0,12 л/м²; пом. 1 (пот.), 2 (пот.), 3 (пот.), 4 (пот.), 5 (пот.), 6 (пот.), 8 (пот.); л. 40, 41 |
| 27 | Краска интерьерная акриловая, матовая, класс истирания 1 | Tikkurila Harmony V503 «Winter» | | | л | 5,51 | 10 | банка 2,7 л | 3 банк | | 22,94 м² × 2 сл. × 0,12 л/м²; пом. 2; л. 40, 41 |
| 28 | Краска интерьерная акриловая, матовая, класс истирания 1 | Tikkurila Luja 7 V503 «Winter» | | | л | 3,10 | 10 | банка 2,7 л | 2 банк | | 12,93 м² × 2 сл. × 0,12 л/м²; пом. 7 (пот.), 9 (пот.); л. 40, 41 |
| 29 | Шпаклёвка финишная полимерная под окраску (стены и потолки, Q3) | по выбору подрядчика | | | м² | 378,91 | 10 | ведро по ТУ | по ТУ | | расход кг/м² на слой — по ТУ; л. 40, 41 |
| 30 | Грунтовка акриловая глубокого проникновения, 2 слоя | по выбору подрядчика | | | м² | 431,84 | 10 | канистра по ТУ | по ТУ | | расход л/м² — по ТУ; л. 40, 41 |
| **Погонажные изделия и потолки** | | | | | | | | | | | |
| 31 | Плинтус напольный МДФ под покраску, h=80 мм, крепление к стене | аналог: плинтус МДФ под покраску 80×16 | | | м.п. | 85,38 | 10 | хлыст 2,4 м | 40 шт | | пом. 1, 2, 3, 4, 5, 8; длина хлыста — по артикулу; л. 40, 41 |
| 32 | Плинтус напольный МДФ под покраску, h=69 мм, крепление к стене | SX165 | | | м.п. | 11,96 | 10 | хлыст 2,4 м | 6 шт | | пом. 6; длина хлыста — по артикулу; л. 40, 41 |

## Примечания

1. Чистое количество — из ведомости объёмов работ и раскладки плитки; запас — отдельной графой (доска — по ведомости отделки, плитка, краска и плинтус — 10 %); «к заказу» — с запасом и кратно упаковке.
2. Плитка — штуками по раскладке, запас на каждую поверхность. Калибр (рабочий размер) и тон — одной партией на помещение, калибр указать при заказе и сверить с раскладкой до укладки.
3. Краска — 0,12 л/м² на слой (середина вилки 0,10–0,15 л/м²) по фактической площади окраски из ведомости отделки; колеровка одной партией.
4. «По ТУ» — расход задаёт производитель выбранного продукта; количество к заказу — после выбора марки.
5. Поз. 3, 4, 6, 31 заданы характеристиками («аналог:»): марку, артикул и поставщика согласовать с заказчиком до закупки, без артикула не заказывать.
6. Штукатурная смесь — на ту же площадь, что строка ВОР «Штукатурка стен» (304,55 м²): площадь одна, расход смеси задаёт производитель.
7. Коробы инсталляции и стояков: ГКЛВ в 2 слоя и профиль 27 × 28 мм считаются по свободным граням коробов (источник — раскладка плиточника и шахты в данных); короб К1 над полом — в спецификации ВК.
8. Потолки ГКЛ: в этой спецификации — площадь системы П113; число листов, профилей и подвесов — по шагам каркаса на листе потолков (подвесы через 1000, несущие через 500, основные через 1200 мм), схема каркаса не выпущена. Сантехника, светильники и мебель — по своим спецификациям.

**Допущения и предложения на листе**

Основа листа: размеры сняты с растрового плана заказчика с частичными размерами: рисунок не в масштабе, помещения выровнены по подписанным размерам мебели и проходов; контрольный обмер не выполнен (К-1); высота потолка 2700 мм принята: на плане заказчика её нет (К-2); толщины стен 300 / 120 мм приняты по плану заказчика, не замерены (К-1); разрешённая мощность 15 кВт принята по типовым ТУ для квартиры, ТУ заказчиком не переданы (К-4).

Знак «**» — предложение проектировщика, заказчиком не утверждено (согласовать с заказчиком): записи в реестре нет: ЩС — щит слаботочный: место и состав; плинтус пом. 1–5, 8, фартук пом. 4 — артикул изделия не выбран: позиция описана характеристиками («аналог по характеристикам»), артикул выбирается при закупке.

См. лист открытых вопросов (лист 6, записи К-1, К-2, К-4).

| Изм. | Кол.уч | Лист | № док. | Подп. | Дата |
|---|---|---|---|---|---|
| Разраб. | | Кырлан А.С. | | | 18.10.26 |
| Пров. | | | | | |
| ГИП | | | | | |
| | | | | | |
| Н. контр. | | | | | |
| Утв. | | | | | |

**ГД-2026-008-АИ**

Квартира с кабинетом

Общая площадь 127,29* м² · * размеры со скана, не замерены (реестр — л. 6, К-1)

| Дизайн-проект интерьера | Стадия | Лист | Листов |
|---|---|---|---|
| | РП | 90 | 92 |

**Спецификация материалов (окончание)**

М б/м

**Кырлан Александр Сергеевич**

# Смета ориентировочная

**ПРЕДВАРИТЕЛЬНО · не для производства работ · открыто пунктов: 4 (реестр — л. 6)**

Работы, материалы, оборудование, услуги и резерв · цены — ориентир по открытым прайсам, не коммерческое предложение

## Сводная смета (цены на 21.09.2026, Москва)

| № | Наименование работ, материалов, услуг | Ед. изм. | Кол-во | Цена за ед., ₽ | Стоимость, ₽ | | | Чей подряд | Срок поставки, дн. | Основание | Источник цены |
|---|---|---|---|---|---|---|---|---|---|---|---|
| | | | | | план | факт | разница | | | | |
| **Работы — по ведомости объёмов работ** | | | | | | | | | | | |
| 1 | Демонтаж и черновые работы (без 5 поз. по КП) | раздел | 1 | | 245 958 | | | бригада | | ВОР, поз. 1–9; л. 86–88 | по ВОР |
| 2 | Инженерные системы (без 12 поз. по КП) | раздел | 1 | | 172 190 | | | бригада | | ВОР, поз. 10–31; л. 86–88 | по ВОР |
| 3 | Чистовые работы (без 1 поз. по КП) | раздел | 1 | | 905 582 | | | бригада, поставщик | | ВОР, поз. 32–49; л. 86–88 | по ВОР |
| **Материалы — по спецификации материалов** | | | | | | | | | | | |
| 4 | Инженерная доска | м² | 114,60 | 4 513 | 517 190 | | | поставщик | | спецификация, поз. 1 | Ц7 |
| 5 | Керамогранит 600×600 мм | м² | 18,00 | 1 800 | 32 400 | | | поставщик | | спецификация, поз. 3 | Ц6 |
| 6 | Керамогранит 600×1200, 1200×600 мм | м² | 83,52 | 3 500 | 292 320 | | | поставщик | | спецификация, поз. 4, 5, 6 | Ц6 |
| 7 | Клей плиточный цементный класса C2 TE S1 | меш. | 22 | 1 800 | 39 600 | | | поставщик | | спецификация, поз. 7 | Ц7 |
| 8 | Затирка цементная класса CG2WA | упак. | 3 | 1 000 | 3 000 | | | поставщик | | спецификация, поз. 8 | Ц7 |
| 9 | Краска Farrow & Ball Modern Emulsion, банка 2,5 л | банк | 25 | 5 800 | 145 000 | | | поставщик | | спецификация, поз. 24, 25 | Ц7 |
| 10 | Краска Tikkurila (Anti-Reflex 2, Harmony, Luja 7), банка 2,7 л | банк | 17 | 3 510 | 59 670 | | | поставщик | | спецификация, поз. 26, 27, 28 | Ц6 |
| 11 | Плинтус напольный МДФ под покраску | шт | 46 | 368 | 16 928 | | | поставщик | | спецификация, поз. 31, 32 | Ц7 |
| 12 | Прочие материалы с расходом по ТУ (клей для доски, гидроизоляция, демпферная лента, смесь для стяжки, смесь штукатурная гипсовая для машинного и ручного нанесения по маякам, лист гклв 12, профиль стальной оцинкованный 27 × 28 мм: каркас коробов (стойки и направляющие), кабель слаботочки, гофра слаботочки, изделия слаботочки, шпаклёвка, грунтовка) | компл | 1 | по КП | | | | поставщик | | спецификация, поз. 2, 9, 10, 11, 12, 13, 14, 15, 16, 17, 18, 19, 20, 21, 22, 23, 29, 30 | |
| **Оборудование и мебель — поставка по спецификациям** | | | | | | | | | | | |
| 13 | Кухонный гарнитур по проекту кухни, изготовление и монтаж (4–8 нед.) | компл | 1 | по КП | | | | поставщик | уточн.; ориентир 4–8 нед. от замера | л. 56, 57 | |

**Допущения и предложения на листе**

Основа листа: размеры сняты с растрового плана заказчика с частичными размерами: рисунок не в масштабе, помещения выровнены по подписанным размерам мебели и проходов; контрольный обмер не выполнен (К-1); высота потолка 2700 мм принята: на плане заказчика её нет (К-2); толщины стен 300 / 120 мм приняты по плану заказчика, не замерены (К-1); разрешённая мощность 15 кВт принята по типовым ТУ для квартиры, ТУ заказчиком не переданы (К-4).

См. лист открытых вопросов (лист 6, записи К-1, К-2, К-4).

| Изм. | Кол.уч | Лист | № док. | Подп. | Дата |
|---|---|---|---|---|---|
| Разраб. | | Кырлан А.С. | | | 18.10.26 |
| Пров. | | | | | |
| ГИП | | | | | |
| | | | | | |
| Н. контр. | | | | | |
| Утв. | | | | | |

**ГД-2026-008-АИ**

Квартира с кабинетом

Общая площадь 127,29* м² · * размеры со скана, не замерены (реестр — л. 6, К-1)

Дизайн-проект интерьера

| Стадия | Лист | Листов |
|---|---|---|
| РП | 91 | 92 |

**Смета ориентировочная**

М б/м

**Кырлан Александр Сергеевич**

# Смета ориентировочная (окончание)

**ПРЕДВАРИТЕЛЬНО · не для производства работ · открыто пунктов: 4 (реестр — л. 6)**

Работы, материалы, оборудование, услуги и резерв · цены — ориентир по открытым прайсам, не коммерческое предложение

## Сводная смета (цены на 21.09.2026, Москва) (продолжение)

| № | Наименование работ, материалов, услуг | Ед. изм. | Кол-во | Цена за ед., ₽ | Стоимость, ₽ | | | Чей подряд | Срок поставки, дн. | Основание | Источник цены |
|---|---|---|---|---|---|---|---|---|---|---|---|
| | | | | | план | факт | разница | | | | |
| 14 | Двери скрытого монтажа с коробом под покраску, поставка | шт | 6 | по КП | | | | поставщик | уточн.; ориентир ≈ 30 дн. | л. 14 | |
| 15 | Оборудование заказчика слаботочных сетей: точка доступа wi-fi — 2 шт; коммутатор — 1 шт | компл | 1 | по КП | | | | заказчик | | л. 23, 24 | |
| 16 | Сантехника, светильники, мебель и предметы интерьера | компл | 1 | по КП | | | | поставщик | | л. 32; л. 33; л. 60; л. 17–19 | |
| **Прочие работы и услуги** | | | | | | | | | | | |
| 17 | Вынос и вывоз строительного мусора | м³ | | по факту | | | | бригада | | после демонтажа | |
| 18 | Подъём материалов на этаж (лифтом или вручную — по договору) | т | | по факту | | | | бригада | | по массе поставки | |
| 19 | Доставка чистовых материалов, 10 % от поставки | | | 10 % | 110 611 | | | поставщик | | от суммы материалов | |
| 20 | Уборка после ремонта | м² | 127,29 | по факту | | | | бригада | | S квартиры | |
| | **Итого работы** | | | | **1 323 730** | | | | | | |
| | **Итого материалы** | | | | **1 106 108** | | | | | | |
| | **Итого прочие услуги** | | | | **110 611** | | | | | | |
| | **Резерв на непредвиденные работы и материалы, 15 %** | | | | **381 067** | | | | | | |
| | **ВСЕГО ориентировочно (без оборудования и позиций по КП)** | | | | **2 921 516** | | | | | | |

## Примечания

1. Смета ориентировочная, не коммерческое предложение: объёмы — из ведомости объёмов работ и спецификации материалов, цены — нижняя граница открытых прайсов Москвы (цены на 21.09.2026); перед договором цены подтвердить у подрядчика и поставщиков.
2. Источники цен: Ц1 — Домашний мастерок: прайс на отделочные работы, 2026; Ц2 — Домашний мастерок: прайс на плиточные работы, 2026; Ц3 Домашний мастерок: прайс на электромонтажные работы, 2026; Ц4 — Профи ремонтник: штукатурно-малярные работы; Ц5 — Profi.ru: укладка керамогранита на стены, Москва 2026; Ц6 — knowledge/spec-materials.md, разд. 1 и 3: ориентир по сегментам; Ц7 — Розница Москвы, 09.2026: Лемана ПРО, KGSnab, официальный дилер Farrow & Ball.
3. В итог не вошли позиции «по КП» и «по факту»: оборудование и мебель, двери, материалы с расходом по ТУ, вывоз мусора, подъём и уборка.
4. Доставка — 10 % от материалов, резерв — 15 % (частный ремонт 10–20 %) отдельными строками, в количествах не спрятаны. Графы «факт» и «разница» заполняются по актам.

**Допущения и предложения на листе**

Основа листа: размеры сняты с растрового плана заказчика с частичными размерами: рисунок не в масштабе, помещения выровнены по подписанным размерам мебели и проходов; контрольный обмер не выполнен (К-1); высота потолка 2700 мм принята: на плане заказчика её нет (К-2); толщины стен 300 / 120 мм приняты по плану заказчика, не замерены (К-1); разрешённая мощность 15 кВт принята по типовым ТУ для квартиры, ТУ заказчиком не переданы (К-4).
См. лист открытых вопросов (лист 6, записи К-1, К-2, К-4).

| Изм. | Кол.уч | Лист | № док. | Подп. | Дата |
|---|---|---|---|---|---|
| Разраб. | | Кырлан А.С. | | | 18.10.26 |
| Пров. | | | | | |
| ГИП | | | | | |
| | | | | | |
| Н. контр. | | | | | |
| Утв. | | | | | |

**ГД-2026-008-АИ**

Квартира с кабинетом

Общая площадь 127,29* м² · * размеры со скана, не замерены (реестр — л. 6, К-1)

Дизайн-проект интерьера

| Стадия | Лист | Листов |
|---|---|---|
| РП | 92 | 92 |

**Смета ориентировочная (окончание)**

М б/м

**Кырлан Александр Сергеевич**

11

# Визуализации

Кырлан Александр Сергеевич

выпуск 18.10.2026 · d2d5a25dca · стр. 105 из 129

выпуск 18.10.2026 № d2d5a25dca · стр. 106 из 129

# Планировочное решение · вид сверху

room-bath1-wB

Квартира с кабинетом · визуализация 2 из 24

room-bath1-wC



выпуск 18.10.2026 № d2d5a25dca · стр. 108 из 129

room-bath1-wD

room-bath2-wC



выпуск 18.10.2026 № d2d5a25dca · стр. 110 из 129

room-bath2-wide

Квартира с кабинетом · визуализация 6 из 24

выпуск 18.10.2026 № d2d5a25dca · стр. 111 из 129

room-bedroom-wA

Квартира с кабинетом · визуализация 7 из 24

выпуск 18.10.2026 № d2d5a25dca · стр. 112 из 129

room-bedroom-wB

Квартира с кабинетом · визуализация 8 из 24

выпуск 18.10.2026 № d2d5a25dca · стр. 113 из 129

room-bedroom-wD



выпуск 18.10.2026 № d2d5a25dca · стр. 114 из 129

room-corridor-wC

Квартира с кабинетом · визуализация 10 из 24

выпуск 18.10.2026 № d2d5a25dca · стр. 115 из 129

room-hall-wB

Квартира с кабинетом · визуализация 11 из 24

выпуск 18.10.2026 № d2d5a25dca · стр. 116 из 129

room-hall-wC



выпуск 18.10.2026 № d2d5a25dca · стр. 117 из 129

room-hall-wD

Квартира с кабинетом · визуализация 13 из 24

выпуск 18.10.2026 № d2d5a25dca · стр. 118 из 129

# room-kids-wA

# room-kids-wB

room-kids-wD

Квартира с кабинетом · визуализация 16 из 24

выпуск 18.10.2026 № d2d5a25dca · стр. 121 из 129

room-living-wA

room-living-wB

Квартира с кабинетом · визуализация 18 из 24

выпуск 18.10.2026 № d2d5a25dca · стр. 123 из 129

room-living-wC



выпуск 18.10.2026 № d2d5a25dca · стр. 124 из 129

room-living-wD

Квартира с кабинетом · визуализация 20 из 24

выпуск 18.10.2026 № d2d5a25dca · стр. 125 из 129

room-study-wA

Квартира с кабинетом · визуализация 21 из 24

выпуск 18.10.2026 № d2d5a25dca · стр. 127 из 129

# room-study-wB

room-study-wD

Квартира с кабинетом · визуализация 23 из 24

room-wardrobe-wide

Квартира с кабинетом · визуализация 24 из 24

выпуск 18.10.2026 № d2d5a25dca · стр. 129 из 129