ДИЗАЙН-ПРОЕКТ ИНТЕРЬЕРА

# Четырёхкомнатная квартира

*13 помещений*

**102,67 м²**

актуальность · комфорт · мягкая геометрия · контраст фактур · открытость · уверенность

60 % — тёплый белый Paper F497 и песочный Castle J484, 30 % — грейж Claystone V486 в фасадах встроенного хранения и текстиле, 10 % — коричнево-лиловый Silhouette L481 из палитры стиля: ТВ-стена зала, изголовья детских, фасад кухонного острова. По практике тёплая аналоговая гамма ровнее держит цвет в квартире с окнами на разные стороны.

ПАЛИТРА 60 / 30 / 10

| F497 | J484 | V486 | L481 |
|---|---|---|---|
| 60 % | 60 % | 30 % | 10 % |



Визуализация 1 · Вид сверху (3D): планировка с мебелью, текстилем и декором

| ОБЪЕКТ | ОБЩАЯ ПЛОЩАДЬ | ПОМЕЩЕНИЙ |
|---|---|---|
| Четырёхкомнатная квартира | 102,67 м² | 13, из них жилых 4 |
| **СТИЛЬ** | **СТАДИЯ** | **ШИФР** |
| Современный (контемпорари) · 13 помещений | Рабочий проект | ГД-2026-004-АИ |

АВТОР ПРОЕКТА

Кырлан Александр Сергеевич

Октябрь 2026

| | | | | | Проект: Четырёхкомнатная квартира | | | |
|---|---|---|---|---|---|---|---|---|
| | Лист | № док. | Подпись | Дата | Титульный лист | Стадия | Лист | Листов |
| Дизайнер | Кырлан А.С. | | | 05.10.26 | | П | 1 | 111 |

выпуск 05.10.2026 № 05166c8858 · стр. 1 из 111

## Список листов

| Лист | Наименование |
|---|---|
| 1 | Титульный лист |
| 2 | Список листов |
| 3 | План планировки от заказчика |
| 4 | План монтажный |
| 5 | Кухня (пом. 6). Монтажная схема |
| 6 | Кухня (пом. 6). Монтажная схема |
| 7 | Шкафы. Монтажная схема. Лист 1 из 3 |
| 8 | Шкафы. Монтажная схема. Лист 2 из 3 |
| 9 | Шкафы. Монтажная схема. Лист 3 из 3 |
| 10 | Карта покрытий стен |
| 11 | Колерная карта |
| 12 | План размещения мебели и оборудования |
| 13 | Спецификация мебели и оборудования |
| 14 | Спецификация мебели и оборудования (продолжение) |
| 15 | Спецификация мебели и оборудования (продолжение) |
| 16 | Спецификация мебели и оборудования (продолжение) |
| 17 | Ведомости изделий, техники и фурнитуры |
| 18 | План выводов сантехники |
| 19 | Схема разводки водопровода и канализации |
| 20 | Спецификация сантехнического оборудования |
| 21 | Раскладка плитки. Ванная комната. Развёртки стен |
| 22 | Раскладка плитки. Санузел. Развёртки стен |
| 23 | План размещения дверей |
| 24 | План потолков |
| 25 | Разрезы и узлы потолков |
| 26 | План розеток и электровыводов |
| 27 | План слаботочных сетей |
| 28 | План освещения |
| 29 | Спецификация светильников и сценарии освещения |
| 30 | Управление светильниками |
| 31 | План вентиляции |
| 32 | План отопления |
| 33 | План покрытий пола |
| 34 | Раскладка плитки. Планы полов |
| 35 | Раскладка плитки. Фартук кухни |
| 36 | Визуализация. Вид сверху |
| 37 | Визуализация: Зал |
| 38 | Визуализация: Зал |
| 39 | Визуализация: Зал |
| 40 | Визуализация: Зал |

| Лист | Наименование |
|---|---|
| 41 | Развёртка стены А. Зал (пом. 1) |
| 42 | Развёртка стены Б. Зал (пом. 1) |
| 43 | Развёртка стены В. Зал (пом. 1) |
| 44 | Развёртка стены Г. Зал (пом. 1) |
| 45 | Визуализация: Ванная комната |
| 46 | Развёртки стен А, Б. Ванная комната (пом. 2) |
| 47 | Развёртки стен В, Г. Ванная комната (пом. 2) |
| 48 | Визуализация: Тёмная комната |
| 49 | Развёртки стен А, Б. Тёмная комната (пом. 3) |
| 50 | Развёртки стен В, Г. Тёмная комната (пом. 3) |
| 51 | Визуализация: Детская 1 |
| 52 | Визуализация: Детская 1 |
| 53 | Развёртка стены А. Детская 1 (пом. 4) |
| 54 | Развёртка стены Б. Детская 1 (пом. 4) |
| 55 | Развёртка стены В. Детская 1 (пом. 4) |
| 56 | Развёртка стены Г. Детская 1 (пом. 4) |
| 57 | Визуализация коридора |
| 58 | Визуализация коридора |
| 59 | Развёртки стен А, Б. Коридор (пом. 5) |
| 60 | Развёртка стены В. Коридор (пом. 5) |
| 61 | Визуализация кухни |
| 62 | Развёртка стены А. Кухня (пом. 6), кухонный фронт |
| 63 | Развёртка стены Б. Кухня (пом. 6) |
| 64 | Развёртка стены В. Кухня (пом. 6) |
| 65 | Развёртка стены Г. Кухня (пом. 6) |
| 66 | Визуализация: Прихожая-коридор |
| 67 | Развёртка стены А. Прихожая-коридор (пом. 7) |
| 68 | Развёртка стены Б. Прихожая-коридор (пом. 7) |
| 69 | Развёртка стены В. Прихожая-коридор (пом. 7) |
| 70 | Развёртка стены Г. Прихожая-коридор (пом. 7) |
| 71 | Визуализация: Гардеробная 2 |
| 72 | Развёртки стен А, Б, В. Гардеробная 2 (пом. 8) |
| 73 | Развёртка стены Г. Гардеробная 2 (пом. 8) |
| 74 | Визуализация: Детская 2 |
| 75 | Визуализация: Детская 2 |
| 76 | Развёртка стены А. Детская 2 (пом. 9) |
| 77 | Развёртка стены Б. Детская 2 (пом. 9) |
| 78 | Развёртка стены В. Детская 2 (пом. 9) |
| 79 | Развёртка стены Г. Детская 2 (пом. 9) |
| 80 | Визуализация санузла |

| Лист | Наименование |
|---|---|
| 81 | Развёртки стен А, Б. Санузел (пом. 10) |
| 82 | Развёртки стен В, Г. Санузел (пом. 10) |
| 83 | Визуализация гостиной |
| 84 | Визуализация гостиной |
| 85 | Развёртка стены А. Гостиная (пом. 11) |
| 86 | Развёртка стены Б. Гостиная (пом. 11) |
| 87 | Развёртки стен В, Г. Гостиная (пом. 11) |
| 88 | Визуализация: Гардеробная 1 |
| 89 | Развёртки стен А, Б. Гардеробная 1 (пом. 12) |
| 90 | Развёртка стены В. Гардеробная 1 (пом. 12) |
| 91 | Визуализация: Балкон 1 |
| 92 | Развёртки стен А, Б. Балкон 1 (пом. 13) |
| 93 | Развёртки стен В, Г. Балкон 1 (пом. 13) |
| Д_1 | Система хранения М_07 |
| Д_2 | Система хранения М_08 |
| Д_3 | Система хранения М_09 |
| Д_4 | Шкаф распашной М_15 |
| Д_5 | Система хранения М_17 |
| Д_6 | Система хранения М_18 |
| Д_7 | Шкаф-купе М_28 |
| Д_8 | Система хранения М_31 |
| Д_9 | Система хранения М_32 |
| Д_10 | Шкаф распашной М_34 |
| Д_11 | Система хранения М_38 |
| Д_12 | Система хранения М_39 |
| Д_13 | Система хранения М_40 |
| Д_14 | Кухня (пом. 6). Развёртка гарнитура |
| Д_15 | Кухня (пом. 6). Развёртка гарнитура |
| С1 | Ведомость отделки помещений. Лист 1 из 2 |
| С2 | Спецификация отделочных материалов |
| С3 | Узлы |

| | Лист | № док. | Подпись | Дата |
|---|---|---|---|---|
| Дизайнер | Кырлан А.О. | | | 05.10.26 |

Проект: Четырёхкомнатная квартира


Список листов

| Стадия | Лист | Листов |
|---|---|---|
| П | 2 | 111 |

выпуск 05.10.2026 № 0516c8858 · стр. 2 из 111

## Отметки по высоте

| | |
|---|---|
| **±0,000** | чистый пол пом. 1, 3–9, 11, 12; отсчёт высот |
| **−0,015** | чистый пол пом. 2, 10, ниже на 15 мм |
| **−0,030** | чистый пол пом. 13, ниже на 30 мм |
| **−0,170** | верх плиты — расчёт, не замер (задание на обмер) |
| **сущ. пол** | снимается до плиты; не замерен (задание на обмер) |

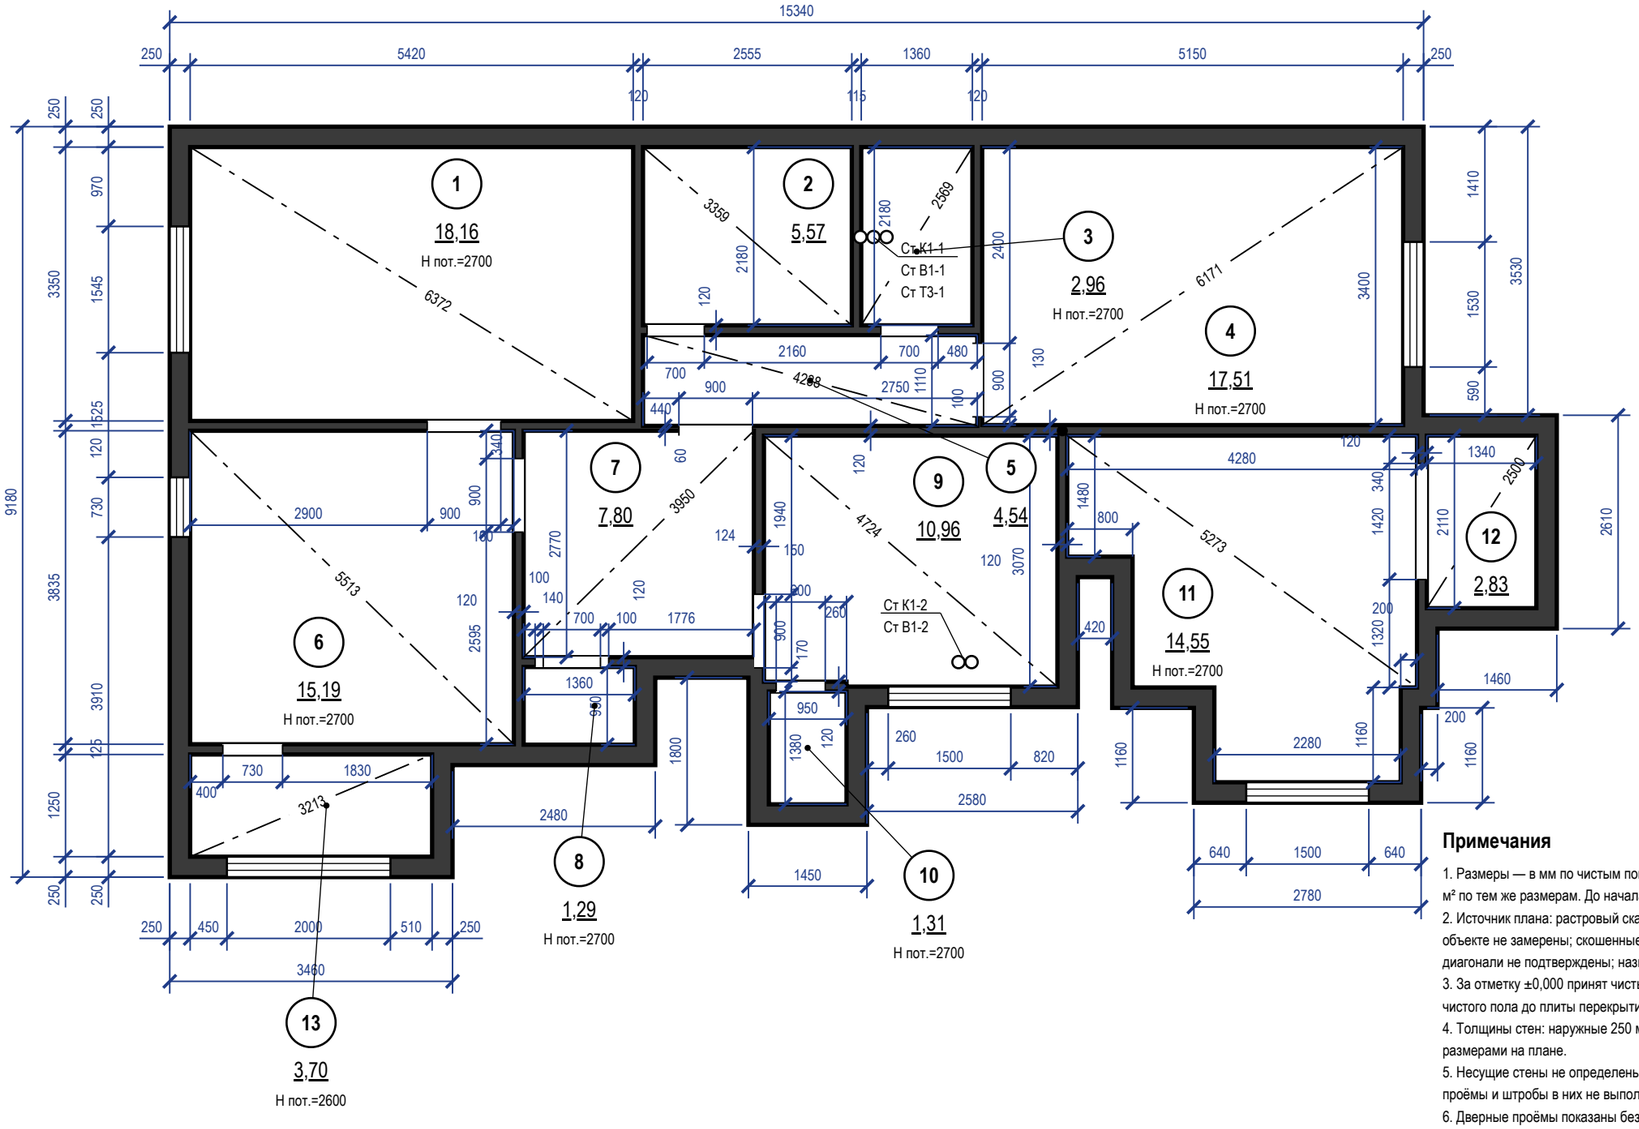


## Экспликация помещений

| № | Наименование | Площадь, м² |
|---|---|---|
| 1 | Зал | 18,16 |
| 2 | Ванная комната | 5,57 |
| 3 | Тёмная комната | 2,96 |
| 4 | Детская 1 | 17,51 |
| 5 | Коридор | 4,54 |
| 6 | Кухня | 15,19 |
| 7 | Прихожая-коридор | 7,80 |
| 8 | Гардеробная 2 | 1,29 |
| 9 | Детская 2 | 10,96 |
| 10 | Санузел | 1,31 |
| 11 | Гостиная | 14,55 |
| 12 | Гардеробная 1 | 2,83 |
| 13 | Балкон 1 * | 3,70 |
| | **Итого (общая площадь)** | **102,67** |

## Условные обозначения


- существующие стены (сечение)
- окно (рама, остекление)
- проём существующий, без заполнения (откосы)
- стояк: К1 — канализация, В1 — ХВС, Т3 — ГВС
- диагональ помещения — контроль прямоугольности
- (1) номер помещения, площадь м²

## Примечания

1. Размеры — в мм по чистым поверхностям стен до отделки (по плану заказчика); площади — в м² по тем же размерам. До начала работ выполнить контрольный обмер.
2. Источник плана: растровый скан плана заказчика, размеры сняты с размерных цепочек, на объекте не замерены; скошенные стены приведены к ступеням (на плане не натура), углы 90° и диагонали не подтверждены; названия и номера помещений со сканом не сверены.
3. За отметку ±0,000 принят чистый пол, не существующий (блок отметок). Н пот. — высота от чистого пола до плиты перекрытия.
4. Толщины стен: наружные 250 мм, перегородки 120 мм; отличающиеся толщины и уступы размерами на плане.
5. Несущие стены не определены: до технического заключения все стены считать несущими; проёмы и штробы в них не выполнять.
6. Дверные проёмы показаны без заполнения (двери — лист 23); высота дверных проёмов 2100 мм; низ окон (подоконник) 800, 900 мм от чистого пола, высота окон 1600, 1700 мм.
7. Диагонали — контрольные размеры; расхождение более 5 мм подписать на плане как перекос.
8. Размеры проверить на месте до начала работ; расхождение контрольных промеров ≤ 2 %.
9. Помещения, отмеченные *, в общую площадь квартиры не входят.
10. Размеры короче 1 мм на листе цепочкой не показаны (две выносные линии на таком расстоянии сливаются): пом. 5, стена А — 50 мм от угла до проёма.

| | | | | | | |
|---|---|---|---|---|---|---|
| | | | | | Проект: Четырёхкомнатная квартира | |
| | Лист | № док. | Подпись | Дата | | |
| Дизайнер | Кырлан А.С. | | | 05.10.26 | План планировки от заказчика | Стадия: П; Лист: 3; Листов: 111 |

выпуск 05.10.2026 № 05166c8858 · стр. 3 из 111

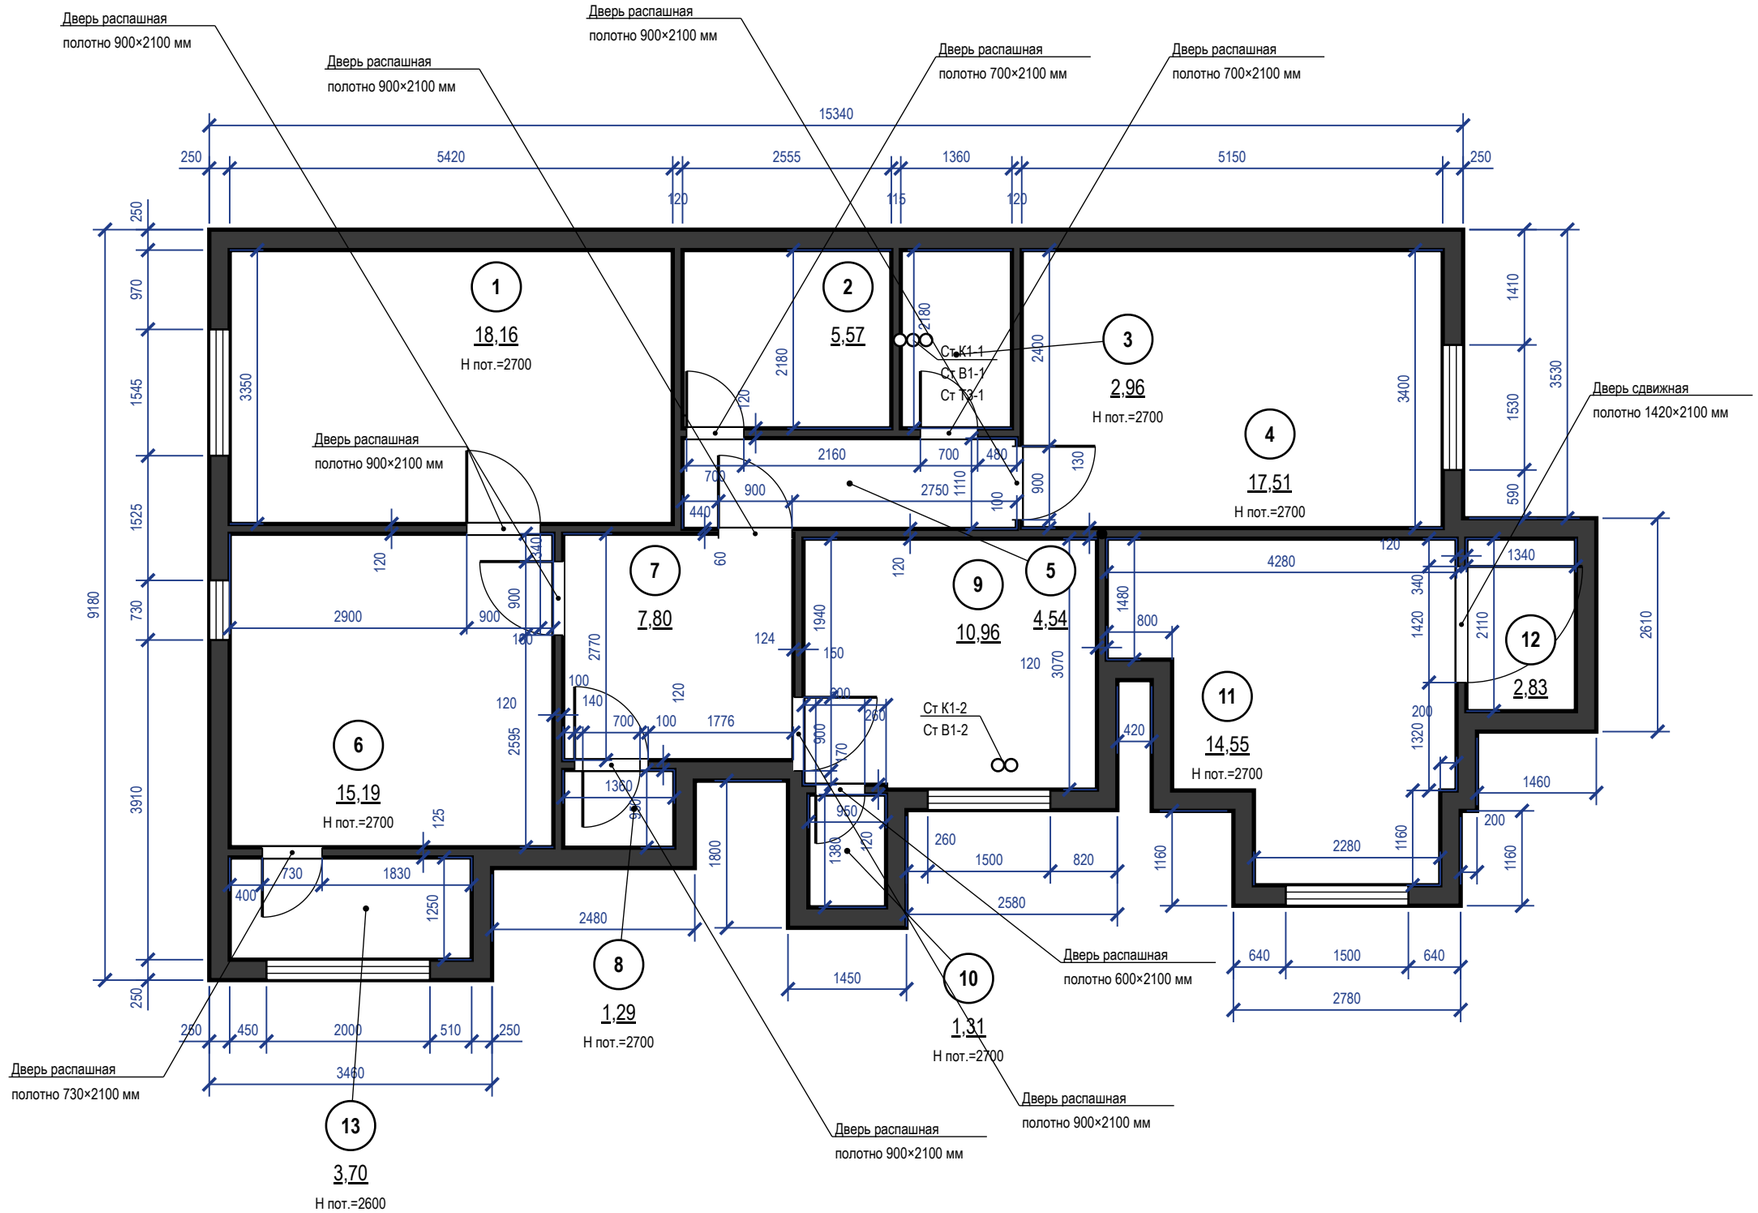


## Экспликация помещений

| № | Наименование | Площадь, м² |
|---|---|---|
| 1 | Зал | 18,16 |
| 2 | Ванная комната | 5,57 |
| 3 | Тёмная комната | 2,96 |
| 4 | Детская 1 | 17,51 |
| 5 | Коридор | 4,54 |
| 6 | Кухня | 15,19 |
| 7 | Прихожая-коридор | 7,80 |
| 8 | Гардеробная 2 | 1,29 |
| 9 | Детская 2 | 10,96 |
| 10 | Санузел | 1,31 |
| 11 | Гостиная | 14,55 |
| 12 | Гардеробная 1 | 2,83 |
| 13 | Балкон 1 * | 3,70 |
| | **Итого (общая площадь)** | **102,67** |

## Примечания


1. Размеры — в мм от чистовых поверхностей стен до отделки; размеры уточнить по месту до начала работ.
2. Новые перегородки и облицовки — синим; каркас и обшивка — по выноскам; двери и проёмы лист 23.
3. Несущие стены не изменять: проёмы, ниши и штробы в них — только по техническому заключению.
4. Размеры короче 1 мм на листе цепочкой не показаны (две выносные линии на таком расстоянии сливаются): пом. 5, стена А — 50 мм от угла до проёма.

| | | | | | |
|---|---|---|---|---|---|
| | | | | | Проект: Четырёхкомнатная квартира |
| | Лист | № док. | Подпись | Дата | |
| Дизайнер | Кырлан А.С. | | | 05.10.26 | План монтажный |


| Стадия | Лист | Листов |
|---|---|---|
| П | 4 | 111 |

выпуск 05.10.2026 № 05166c8858 · стр. 4 из 111

## Привязка выводов и крепление модулей

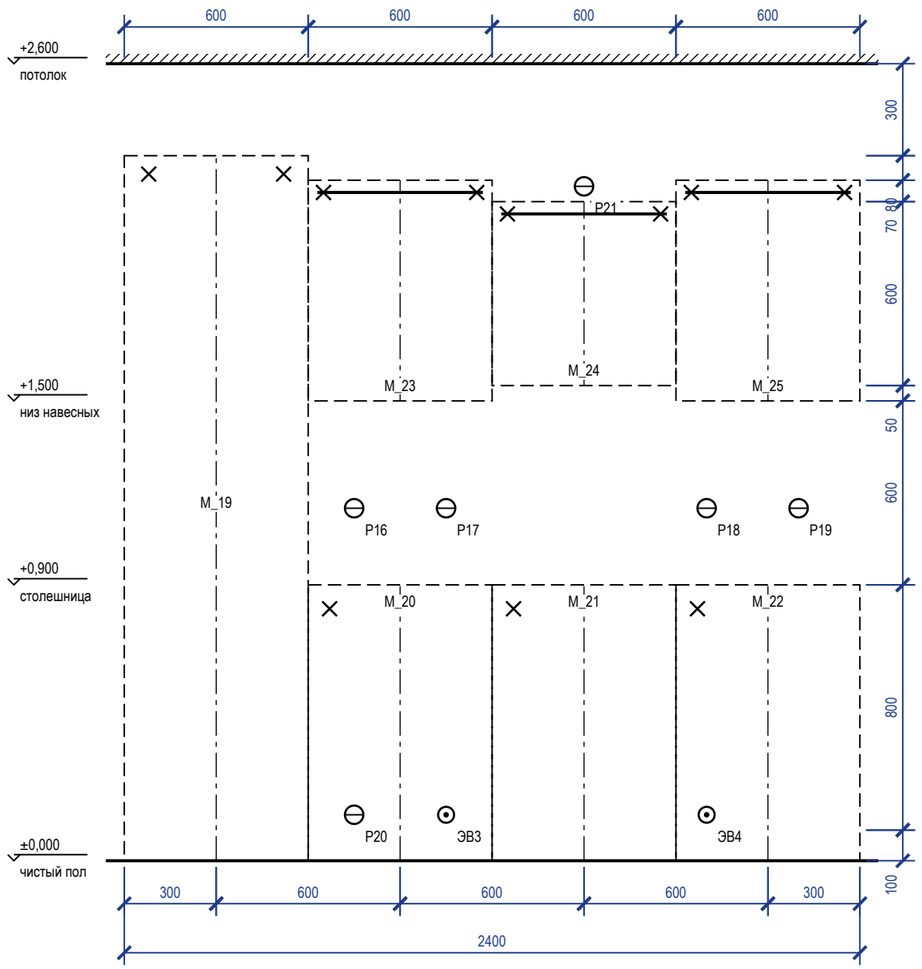


## План столешницы

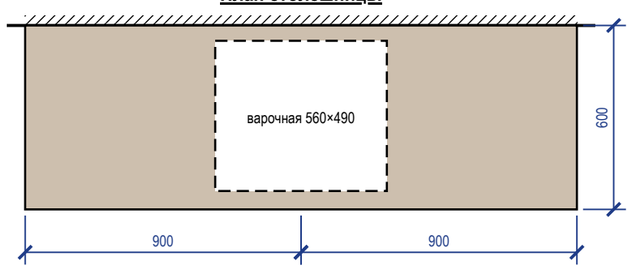


## Привязка выводов к осям модулей

| Код | Назначение | Модуль | От оси, мм | H, мм | Размещение |
|---|---|---|---|---|---|
| P16 | розетка ×2 — фартук: мелкая техника | M_20 | −150 | 1150 | над столешницей (фартук) |
| P20 | розетка — холодильник встроенный M_19 (розетка в модуле M_20) | M_20 | −150 | 150 | в соседнем модуле, за ящиком |
| P17 | розетка ×2 — фартук: мелкая техника | M_20 | +150 | 1150 | над столешницей (фартук) |
| ЭВ3 | вывод кабеля — варочная панель M_21 | M_20 | +150 | 150 | в соседнем модуле, за ящиком |
| P21 | розетка — вытяжка M_24 (в модуле, съёмная панель) | M_24 | 0 | 2200 | в навесном модуле |
| P18 | розетка ×2 — фартук: мелкая техника | M_22 | −200 | 1150 | над столешницей (фартук) |
| ЭВ4 | вывод кабеля — духовой шкаф M_21 (вывод в соседнем модуле M_22) | M_22 | −200 | 150 | в соседнем модуле, за ящиком |
| P19 | розетка ×2 — фартук: мелкая техника | M_22 | +100 | 1150 | над столешницей (фартук) |

## Зазоры под отделку

| Поверхность | Отделка | Зазор, мм | Учесть |
|---|---|---|---|
| фартук | керамогранит | 10 | от чернового основания до корпуса навесных и столешницы |
| стены | окраска | 5 | под штукатурку и шпаклёвку за пеналом |
| пол | инженерная доска | | цоколь — после укладки пола, опоры ±20 мм |

## Условные обозначения

- навесной модуль (невидимый контур)
- ось модуля (от неё — привязка вывода)
- анкер / уголок крепления к стене
- розетка на стене
- вывод кабеля к технике
- B1 — вывод воды B1 / Т3, канализации К1

## Примечания


1. Выводы — по проекту электрики и ВК; привязка по горизонтали — от оси модуля (плюс — вправо по виду), по высоте — от чистого пола до оси вывода.
2. Пенал — уголки к стене 2 шт. сверху; нижние модули — стяжками между собой и уголком к стене; ряд выставить по уровню опорами цоколя.
3. Розетки над столешницей — не ниже 150 мм над ней и не за корпусом техники; розетка за ПММ, духовым шкафом и холодильником — только в соседнем модуле или в зоне цоколя с доступом.
4. Столешница — вырезы по шаблонам выбранных моделей мойки и варочной панели; торцы у стены — герметик, пристеночный плинтус.

| | | | | | |
|---|---|---|---|---|---|
| | | | | | Проект: Четырёхкомнатная квартира |
| | Лист | № док. | Подпись | Дата | |
| Дизайнер | Кырлан А.С. | | | 05.10.26 | Кухня (пом. 6). Монтажная схема |

| Стадия | Лист | Листов |
|---|---|---|
| П | 5 | 111 |

выпуск 05.10.2026 № 05166c8858 · стр. 5 из 111

## Привязка выводов и крепление модулей

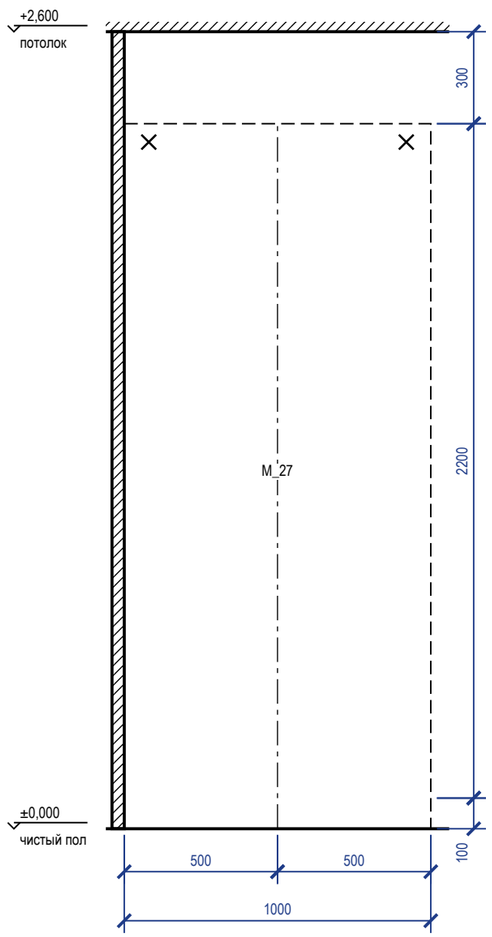


### Привязка выводов к осям модулей

| Код | Назначение | Модуль | От оси, мм | H, мм | Размещение |
|---|---|---|---|---|---|

### Зазоры под отделку

| Поверхность | Отделка | Зазор, мм | Учесть |
|---|---|---|---|
| фартук | керамогранит | 10 | от чернового основания до корпуса навесных и столешницы |
| стены | окраска | 5 | под штукатурку и шпаклёвку за пеналом |
| пол | инженерная доска | | цоколь — после укладки пола, опоры ±20 мм |

### Условные обозначения

- навесной модуль (невидимый контур)
- ось модуля (от неё — привязка вывода)
- анкер / уголок крепления к стене
- розетка на стене
- вывод кабеля к технике
- B1 — вывод воды B1 / Т3, канализации К1

### Примечания


1. Выводы — по проекту электрики и ВК; привязка по горизонтали — от оси модуля (плюс — вправо по виду), по высоте — от чистого пола до оси вывода.
2. Пенал — уголки к стене 2 шт. сверху; нижние модули — стяжками между собой и уголком к стене; ряд выставить по уровню опорами цоколя.
3. Розетки над столешницей — не ниже 150 мм над ней и не за корпусом техники; розетка за ПММ, духовым шкафом и холодильником — только в соседнем модуле или в зоне цоколя с доступом.
4. Столешница — вырезы по шаблонам выбранных моделей мойки и варочной панели; торцы у стены — герметик, пристеночный плинтус.

| | | | | | |
|---|---|---|---|---|---|
| | | | | | Проект: Четырёхкомнатная квартира |
| | Лист | № док. | Подпись | Дата | |
| Дизайнер | Кырлан А.С. | | | 05.10.26 | Кухня (пом. 6). Монтажная схема |


| Стадия | Лист | Листов |
|---|---|---|
| П | 6 | 111 |

выпуск 05.10.2026 № 05166c8858 · стр. 6 из 111


### М_07 (пом. 2)

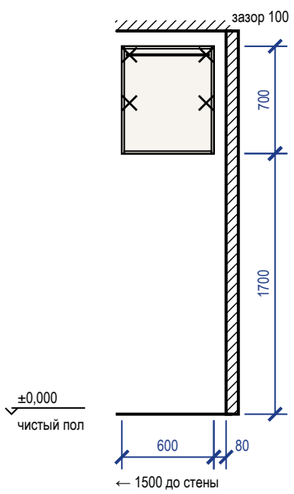



### Система хранения М_08 (пом. 3)

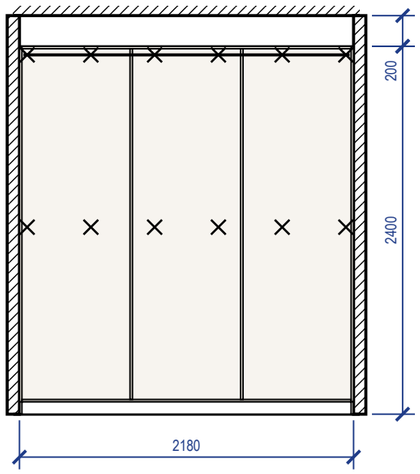



### Система хранения М_09 (пом. 3)

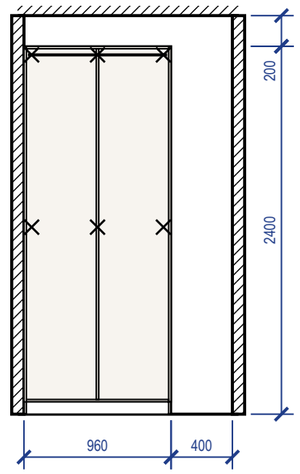


### Шкаф распашной М_15 (пом. 4)

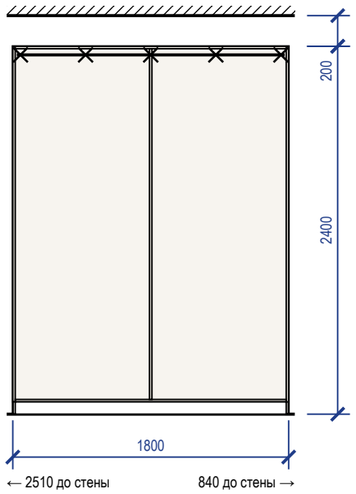


### Система хранения М_17 (пом. 4)

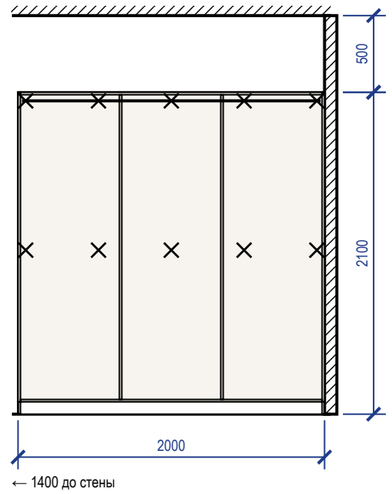


## Крепление и зазоры под отделку (изделия листа 1)

| Марка | Помещение, стена | Основание | Отделка стены | Зазор, мм | Крепёж по планке | От опрокидывания |
|---|---|---|---|---|---|---|
| М_07 | Ванная комната (2), стена Б | по основанию — см. таблицу крепежа | плитка | 10 | анкер 4 шт. (2 ряда) | крепление к стене, 2 точки |
| М_08 | Тёмная комната (3), стена Б | по основанию — см. таблицу крепежа | окраска | 5 | анкер 12 шт. (2 ряда) | крепление к стене, 4 точки |
| М_09 | Тёмная комната (3), стена А | по основанию — см. таблицу крепежа | окраска | 5 | анкер 6 шт. (2 ряда) | крепление к стене, 3 точки |
| М_15 | Детская 1 (4), стена В | по основанию — см. таблицу крепежа | окраска | 5 | анкер 5 шт., шаг 425 | уголок к стене, 3 шт. |
| М_17 | Детская 1 (4), стена Г | по основанию — см. таблицу крепежа | окраска | 5 | анкер 10 шт. (2 ряда) | крепление к стене, 3 точки |

## Крепёж по основанию стены

| Основание стены | Крепёж |
|---|---|
| бетон, ж/б | анкер-шуруп 7,5×72 или дюбель 8×60 с шурупом 5×70 |
| кирпич полнотелый | дюбель 8×80 с шурупом 5×90 |
| газобетон, пазогребень | дюбель для газобетона 10×100 или химический анкер |
| гипсокартон | закладная до обшивки (брус 40×80 или фанера 18 мм), саморез в закладную |

## Условные обозначения

- × — анкер / уголок крепления к стене
- корпус и полки ЛДСП (вид на стену)
- компенсатор — короб до потолка

## Примечания


1. Установочные размеры — от чистого пола и чистых стен; перед установкой контрольный замер после отделки.
2. Порядок: корпус выставить по уровню опорами цоколя → закрепить к стене по задней планке → навесить двери и фасады, отрегулировать зазоры → подогнать и закрепить компенсатор.
3. Анкеры — с шагом не более 500 мм, не ближе 50 мм от края планки; на ГКЛ только в закладную, установленную до обшивки.
4. Скрытые коммуникации под анкеры проверить детектором; трассы электрики по плану розеток.
5. Монтажная схема на 3 листах, лист 1 из 3; продолжение — на следующем листе схемы. Условные обозначения, таблица крепежа по основанию и примечания повторены на каждом листе.

| | | | | | |
|---|---|---|---|---|---|
| | | | | | Проект: Четырёхкомнатная квартира |
| | Лист | № док. | Подпись | Дата | |
| Дизайнер | Кырлан А.С. | | | 05.10.26 | Шкафы. Монтажная схема. Лист 1 из 3 |


| Стадия | Лист | Листов |
|---|---|---|
| П | 7 | 111 |

выпуск 05.10.2026 № 05166c8858 · стр. 7 из 111


**Система хранения М_18 (пом. 5)**

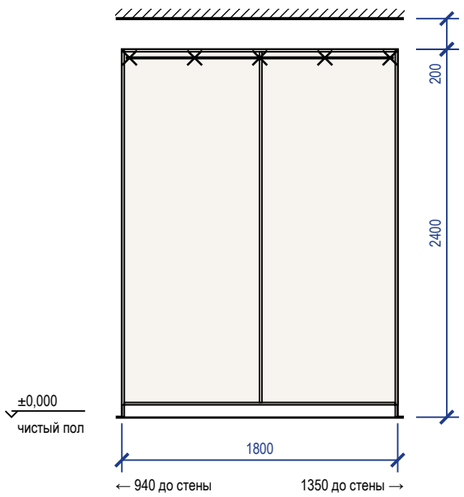



**Шкаф-купе М_28 (пом. 7)**

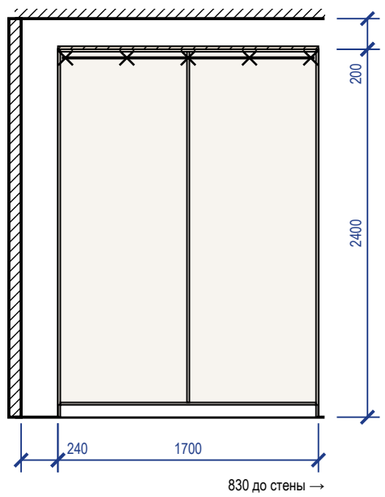



**Система хранения М_31 пом. 8**

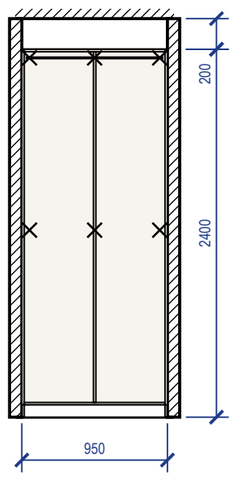


**Система хранения М_32 (пом. 8)**

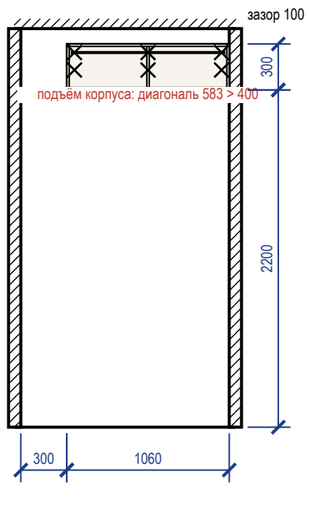


**Шкаф распашной М_34 (пом. 9)**

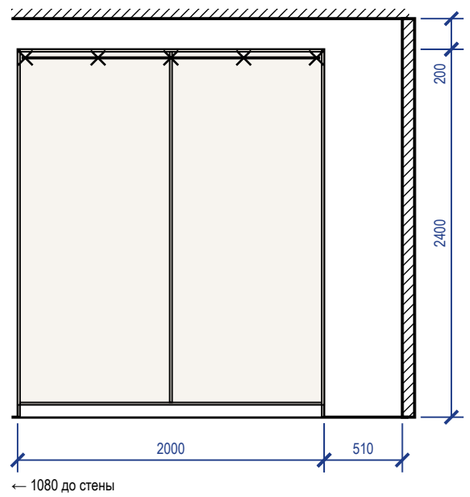


## Крепление и зазоры под отделку (изделия листа 2)

| Марка | Помещение, стена | Основание | Отделка стены | Зазор, мм | Крепёж по планке | От опрокидывания |
|---|---|---|---|---|---|---|
| М_18 | Коридор (5), стена А | по основанию — см. таблицу крепежа | окраска | 5 | анкер 5 шт., шаг 425 | крепление к стене, 4 точки |
| М_28 | Прихожая-коридор (7), стена Б | по основанию — см. таблицу крепежа | окраска | 5 | анкер 5 шт., шаг 400 | крепление к стене, 3 точки |
| М_31 | Гардеробная 2 (8), стена Б | по основанию — см. таблицу крепежа | окраска | 5 | анкер 6 шт. (2 ряда) | крепление к стене, 3 точки |
| М_32 | Гардеробная 2 (8), стена В | по основанию — см. таблицу крепежа | окраска | 5 | анкер 6 шт. (2 ряда) | крепление к стене, 4 точки |
| М_34 | Детская 2 (9), стена А | по основанию — см. таблицу крепежа | окраска | 5 | анкер 5 шт., шаг 475 | уголок к стене, 3 шт. |

## Крепёж по основанию стены

| Основание стены | Крепёж |
|---|---|
| бетон, ж/б | анкер-шуруп 7,5×72 или дюбель 8×60 с шурупом 5×70 |
| кирпич полнотелый | дюбель 8×80 с шурупом 5×90 |
| газобетон, пазогребень | дюбель для газобетона 10×100 или химический анкер |
| гипсокартон | закладная до обшивки (брус 40×80 или фанера 18 мм), саморез в закладную |

## Условные обозначения

- анкер / уголок крепления к стене
- корпус и полки ЛДСП (вид на стену)
- компенсатор — короб до потолка

## Примечания


1. Установочные размеры — от чистого пола и чистых стен; перед установкой контрольный замер после отделки.
2. Порядок: корпус выставить по уровню опорами цоколя → закрепить к стене по задней планке → навесить двери и фасады, отрегулировать зазоры → подогнать и закрепить компенсатор.
3. Анкеры — с шагом не более 500 мм, не ближе 50 мм от края планки; на ГКЛ только в закладную, установленную до обшивки.
4. Скрытые коммуникации под анкеры проверить детектором; трассы электрики по плану розеток.
5. Монтажная схема на 3 листах, лист 2 из 3; продолжение — на следующем листе схемы. Условные обозначения, таблица крепежа по основанию и примечания повторены на каждом листе.

| | | | | | |
|---|---|---|---|---|---|
| | | | | | Проект: Четырёхкомнатная квартира |
| | Лист | № док. | Подпись | Дата | |
| Дизайнер | Кырлан А.С. | | | 05.10.26 | Шкафы. Монтажная схема. Лист 2 из 3 |


| Стадия | Лист | Листов |
|---|---|---|
| П | 8 | 111 |

выпуск 05.10.2026 № 05166c8858 · стр. 8 из 111


**Система хранения М_38 (пом. 12)**

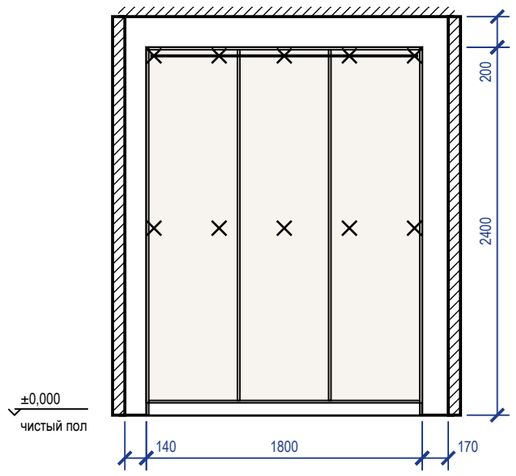


**Система хранения М_39 пом. 13**

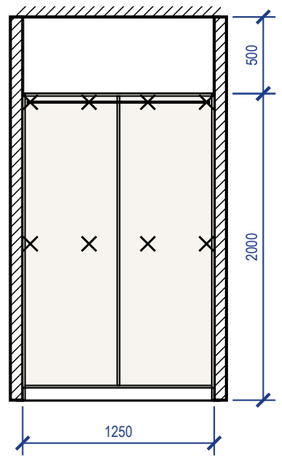


**Система хранения М_40 пом. 13**

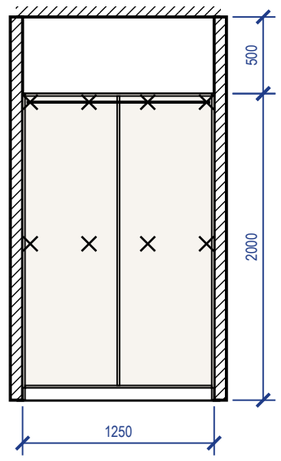


## Крепление и зазоры под отделку (изделия листа 3)

| Марка | Помещение, стена | Основание | Отделка стены | Зазор, мм | Крепёж по планке | От опрокидывания |
|---|---|---|---|---|---|---|
| М_38 | Гардеробная 1 (12), стена Б | по основанию — см. таблицу крепежа | окраска | 5 | анкер 10 шт. (2 ряда) | крепление к стене, 4 точки |
| М_39 | Балкон 1 (13), стена Б | по основанию — см. таблицу крепежа | окраска | 5 | анкер 8 шт. (2 ряда) | крепление к стене, 3 точки |
| М_40 | Балкон 1 (13), стена Г | по основанию — см. таблицу крепежа | окраска | 5 | анкер 8 шт. (2 ряда) | крепление к стене, 3 точки |

## Крепёж по основанию стены

| Основание стены | Крепёж |
|---|---|
| бетон, ж/б | анкер-шуруп 7,5×72 или дюбель 8×60 с шурупом 5×70 |
| кирпич полнотелый | дюбель 8×80 с шурупом 5×90 |
| газобетон, пазогребень | дюбель для газобетона 10×100 или химический анкер |
| гипсокартон | закладная до обшивки (брус 40×80 или фанера 18 мм), саморез в закладную |

## Условные обозначения


- анкер / уголок крепления к стене
- корпус и полки ЛДСП (вид на стену)
- компенсатор — короб до потолка

## Примечания

1. Установочные размеры — от чистого пола и чистых стен; перед установкой контрольный замер после отделки.
2. Порядок: корпус выставить по уровню опорами цоколя → закрепить к стене по задней планке → навесить двери и фасады, отрегулировать зазоры → подогнать и закрепить компенсатор.
3. Анкеры — с шагом не более 500 мм, не ближе 50 мм от края планки; на ГКЛ только в закладную, установленную до обшивки.
4. Скрытые коммуникации под анкеры проверить детектором; трассы электрики по плану розеток.
5. Монтажная схема на 3 листах, лист 3 из 3. Условные обозначения, таблица крепежа по основанию и примечания повторены на каждом листе.

| | | | | | Проект: Четырёхкомнатная квартира | | | |
|---|---|---|---|---|---|---|---|---|
| | Лист | № док. | Подпись | Дата | Шкафы. Монтажная схема. Лист 3 из 3 | Стадия | Лист | Листов |
| Дизайнер | Кырлан А.С. | | | 05.10.26 | | П | 9 | 111 |

выпуск 05.10.2026 № 05166c8858 · стр. 9 из 111

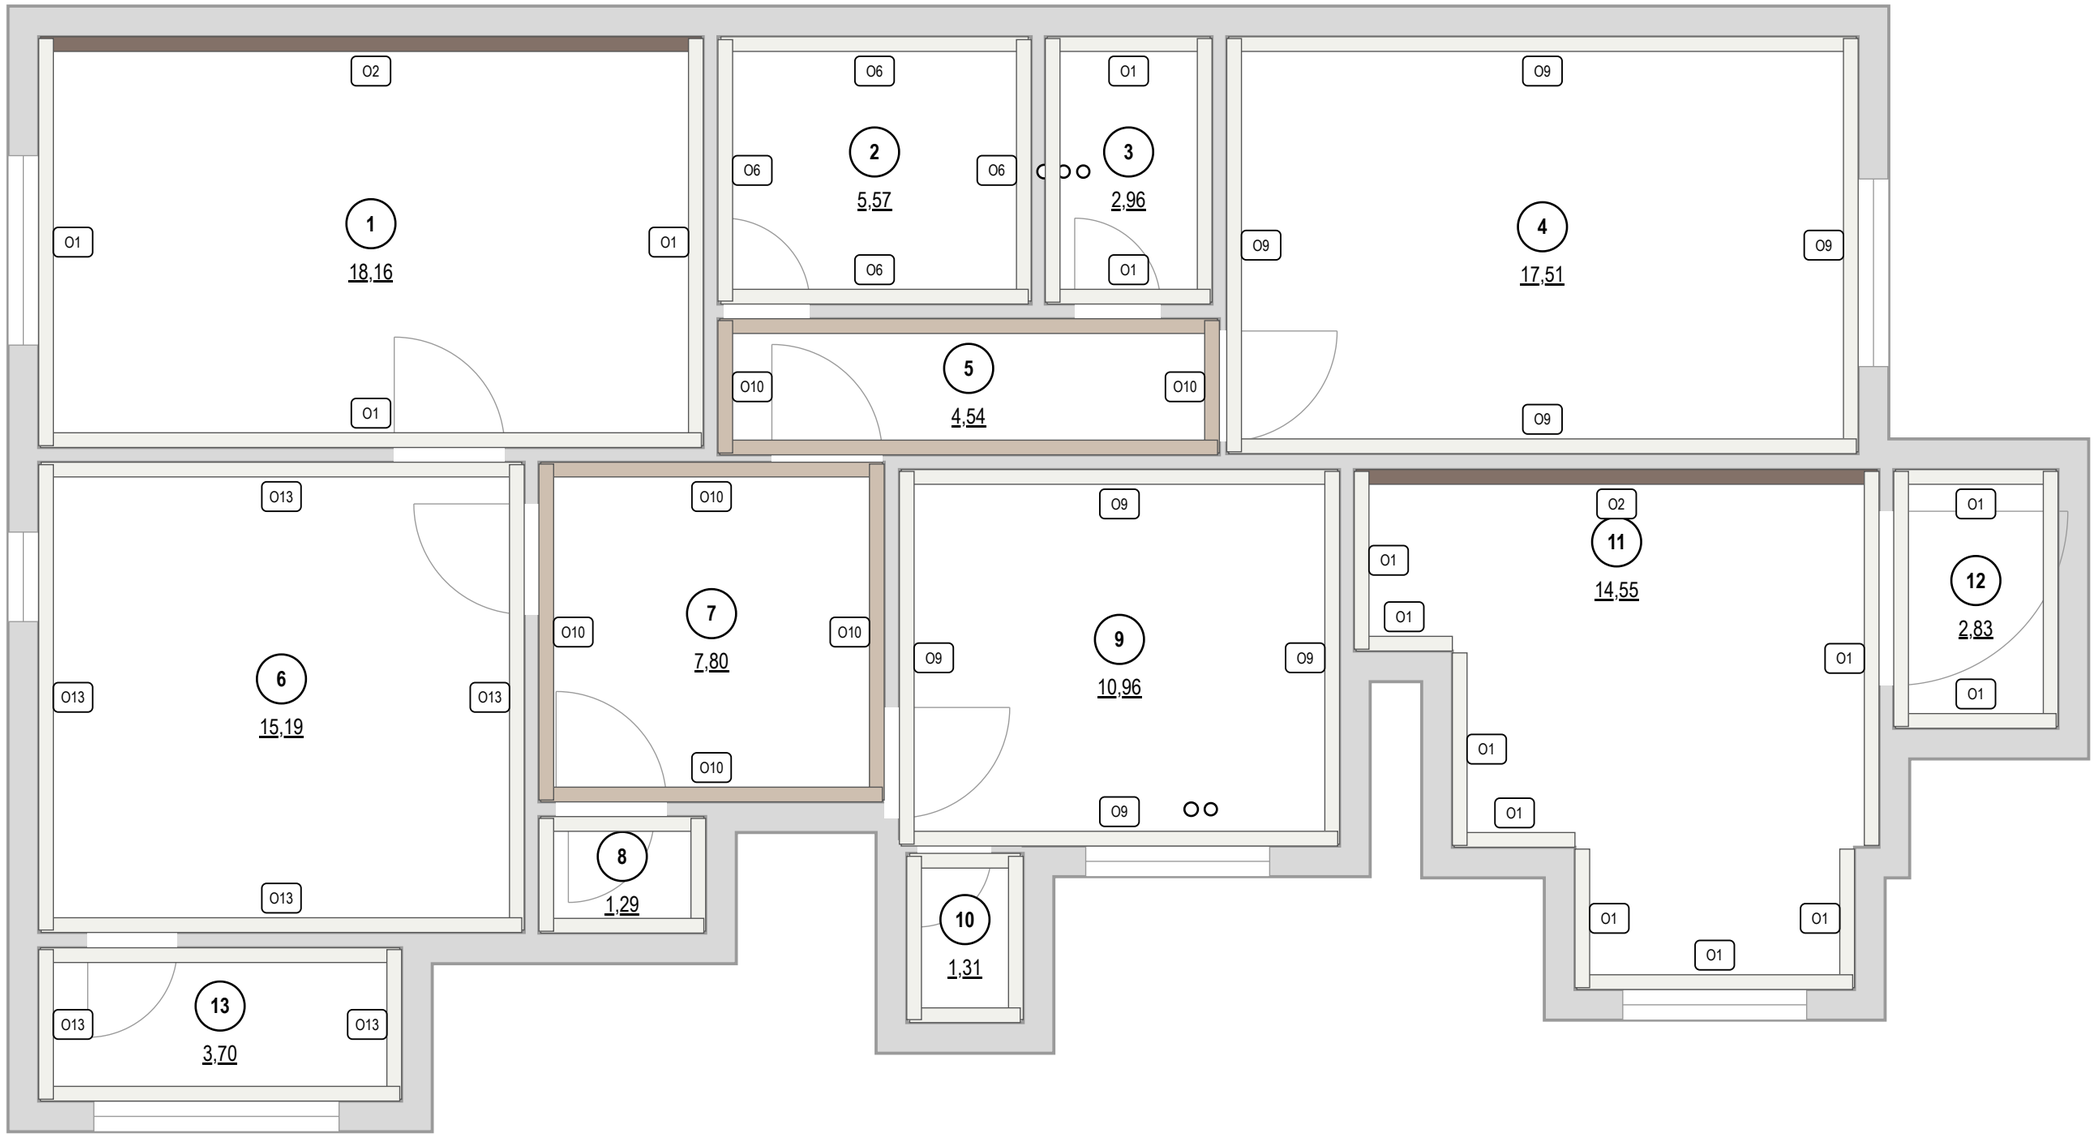


**Покрытия стен**

| Марка | Покрытие | Помещение: S, м² | Итого, м² |
|---|---|---|---|
| O1 | окраска Tikkurila · F497 «Paper» | 1: 25,7; 3: 16,6; 8: 8,3; 11: 25,5; 12: 14,6 | 90,8 |
| O2 | окраска Tikkurila · L481 «Silhouette» | 1: 13,5; 11: 10,6 | 24,1 |
| O6 | облицовка плиткой · «тон Paper F497» 600×600 мм | 2: 21,9; 10: 10,0 | 31,8 |
| O9 | окраска Tikkurila · F497 «Paper» | 4: 39,8; 9: 28,8 | 68,6 |
| O10 | окраска Tikkurila · J484 «Castle» | 5: 20,0; 7: 20,0 | 40,0 |
| O13 | окраска Tikkurila · F497 «Paper» | 6: 32,6; 13: 16,2 | 48,8 |

| | | | | | |
|---|---|---|---|---|---|
| | | | | | Проект: Четырёхкомнатная квартира |
| | Лист | № док. | Подпись | Дата | |
| Дизайнер | Кырлан А.С. | | | 05.10.26 | Карта покрытий стен |

| Стадия | Лист | Листов |
|---|---|---|
| П | 10 | 111 |

Площади — нетто, по развёрткам (за вычетом проёмов и фартука); высоты помещений — от чистого пола.

выпуск 05.10.2026 № 05166c8858 · стр. 10 из 111

## Колерная карта по помещениям

| Помещение | Поверхность | Образец | Поз. | Система и код цвета | Производитель, линейка / материал, артикул | Блеск | Класс EN 13300 | LRV | Площадь |
|---|---|---|---|---|---|---|---|---|---|
| **1. Зал** 18,16 м² | стены | | **К1** | Tikkurila F497 | Tikkurila · Optiva 5 Matt | матовая | 2 | 88 | 25,9 м² |
| | акцент А | | **К2** | Tikkurila L481 | Tikkurila · Optiva 5 Matt | матовая | 2 | 18 | 13,6 м² |
| | потолок | | **К3** | Tikkurila F497 | Tikkurila · Anti-Reflex 2 | глубокомат. | 2 | 88 | 18,2 м² |
| | пол | | **КМ1** | по образцу | инженерная доска · аналог по хар. | | | | 18,2 м² |
| | плинтус | | **К4** | Tikkurila F497 | МДФ · в цвет Tikkurila | полуглянц. | 2 | 88 | 16,6 м |
| **2. Ванная комната** 5,57 м² | стены | | **КМ2** | тон Paper F497 (тёплый белый) | плитка · аналог по хар. | | | | 22,3 м² |
| | потолок | | **К5** | Tikkurila F497 | Tikkurila · Luja 7 | матовая | 1 | 88 | 5,6 м² |
| | пол | | **КМ3** | тон Castle J484 (тёплый песочный) | керамогранит · аналог по хар. | | | | 5,6 м² |
| **3. Тёмная комната** 2,96 м² | стены | | **К1** | Tikkurila F497 | Tikkurila · Optiva 5 Matt | матовая | 2 | 88 | 16,9 м² |
| | потолок | | **К3** | Tikkurila F497 | Tikkurila · Anti-Reflex 2 | глубокомат. | 2 | 88 | 3,0 м² |
| | пол | | **КМ1** | по образцу | инженерная доска · аналог по хар. | | | | 3,0 м² |
| | плинтус | | **К4** | Tikkurila F497 | МДФ · в цвет Tikkurila | полуглянц. | 2 | 88 | 6,4 м |
| **4. Детская 1** 17,51 м² | стены | | **К6** | Tikkurila F497 | Tikkurila · Joker | полуматов. | 2 | 88 | 40,1 м² |
| | потолок | | **К3** | Tikkurila F497 | Tikkurila · Anti-Reflex 2 | глубокомат. | 2 | 88 | 17,5 м² |
| | пол | | **КМ1** | по образцу | инженерная доска · аналог по хар. | | | | 17,5 м² |
| | плинтус | | **К4** | Tikkurila F497 | МДФ · в цвет Tikkurila | полуглянц. | 2 | 88 | 16,2 м |
| **5. Коридор** 4,54 м² | стены | | **К7** | Tikkurila J484 | Tikkurila · Optiva 20 Semimatt | полуматов. | 2 | 55 | 22,2 м² |
| | потолок | | **К3** | Tikkurila F497 | Tikkurila · Anti-Reflex 2 | глубокомат. | 2 | 88 | 4,5 м² |
| | пол | | **КМ4** | тон Claystone V486 (грейж) | керамогранит · аналог по хар. | | | | 4,5 м² |
| | плинтус | | **К8** | Tikkurila J484 | МДФ · в цвет Tikkurila | полуглянц. | 2 | 55 | 8,1 м |
| **6. Кухня** 15,19 м² | стены | | **К9** | Tikkurila F497 | Tikkurila · Luja 7 | полуматов. | 1 | 88 | 34,5 м² |
| | потолок | | **К5** | Tikkurila F497 | Tikkurila · Luja 7 | матовая | 1 | 88 | 15,2 м² |
| | пол | | **КМ1** | по образцу | инженерная доска · аналог по хар. | | | | 15,2 м² |
| | плинтус | | **К4** | Tikkurila F497 | МДФ · в цвет Tikkurila | полуглянц. | 2 | 88 | 13,8 м |
| | фартук | | **КМ5** | тон Paper F497 (тёплый белый) | керамогранит · аналог по хар. | | | | 1,1 м² |

## Схема палитры проекта

Стиль: Современный (контемпорари) · схема: аналоговая

| основной | основной | второстепенный | акцентный |
|---|---|---|---|
| **Tikkurila F497** | **Tikkurila J484** | **Tikkurila V486** | **Tikkurila L481** |
| Paper<br>LRV 88<br>стены 1,3,4,6,8,9,11,12,13;<br>потолок<br>1,2,3,4,5,6,7,8,9,10,11,12,13;<br>плинтус 1,3,4,6,8,9,11,12; текстиль/декор 1 | Castle<br>LRV 55<br>стены 5,7; плинтус 5,7;<br>текстиль/декор 1,6 | Claystone<br>LRV 44<br>текстиль/декор 1,13 | Silhouette<br>LRV 18<br>акцент 1,11; текстиль/декор<br>1,11 |

План 60/30/10

| 60% | 30% | 10% |
|---|---|---|

Окраска, факт — по площади стен, акцентов, потолков

| 94% | 6% |
|---|---|

окрашено всего 389,8 м²; второстепенный тон несут мебель и текстиль

**Текстиль и декор в цветах вне палитры проекта**

- NCS S 3005-Y20R тёплый тауп-серый — пом. 1 (Т3), 7 (Т15), 9 (Т18)
- Tikkurila H487 Pumice — пом. 1 (Т4), 4 (Т9, Т10, Т11), 9 (Т17, Т19)
- Tikkurila V484 Driftwood — пом. 4 (Т8), 9 (Т16), 13 (Т23)
- NCS S 5010-B10G серо-петроль — пом. 4 (Т12, Т13)
- Farrow & Ball No. 47 Green Smoke — пом. 9 (Т20, Т21)

## Условные обозначения

- **К1** Tikkurila F497 · Paper · Optiva 5 Matt · матовая · кл. 2
- **К2** Tikkurila L481 · Silhouette · Optiva 5 Matt · матовая · кл. 2
- **К3** Tikkurila F497 · Paper · Anti-Reflex 2 · глубокомат. · кл. 2
- **К4** Tikkurila F497 · Paper · МДФ · полуглянц. · кл. 2
- **К5** Tikkurila F497 · Paper · Luja 7 · матовая · кл. 1
- **К6** Tikkurila F497 · Paper · Joker · полуматов. · кл. 2
- **К7** Tikkurila J484 · Castle · Optiva 20 Semimatt · полуматов. · кл. 2
- **К8** Tikkurila J484 · Castle · МДФ · полуглянц. · кл. 2
- **К9** Tikkurila F497 · Paper · Luja 7 · полуматов. · кл. 1
- дерево (доска, паркет, ламинат) — рисунок досок
- керамогранит, плитка, камень — сетка швов по формату


- **КМ1** инженерная доска · аналог: дуб натуральный брашированный, масло-воск, 14/4 мм
- **КМ2** плитка · аналог: керамогранит матовый, тон F497, 600×600×9 мм
- **КМ3** аналог: керамогранит матовый R10, тон J484, 600×600×10 мм
- **КМ4** аналог: керамогранит матовый R10, тон V486, 600×600×10 мм
- **КМ5** аналог: керамогранит матовый, тон F497, 600×600×9 мм
- **КМ6** аналог: керамогранит матовый R11, тон V486, 600×600×10 мм
- **КМ7** керамогранит · аналог: плинтус из керамогранита пола, подрезка 80 мм, верхняя кромка с запилом 45°

К — позиция окраски (код + продукт + блеск), КМ — позиция материала, тон КМ — по описанию артикула, эталон — образец материала; ≈ LRV — расчёт по HEX, справочно

## Примечания

1. Цвет утверждается только по выкрасу на объекте: формат от А3 до 1000×1000 мм на загрунтованном ГКЛ, в 2 слоя (как на стене), не на белой шпаклёвке; смотреть днём и при свете проекта своего помещения, рядом с образцами пола и фасадов. Подпись на обороте: код, бренд и веер, дата.
2. Колеровка машинная в колеровочном центре бренда; каждый код — за один проход, одной партией на весь объём. Колеровщику передаётся только система и код утверждённого веера; плашки и HEX на листе — ориентир, печать не является эталоном цвета.
3. Класс мокрого истирания — EN 13300 (ISO 11998); блеск — по ГОСТ 31975 (ISO 2813), геометрия 60°. LRV — пересчёт координаты L каталога производителя (Y = ((L*+16)/116)³); «≈» — расчёт по HEX, справочно.
4. Площади поверхностей — тем же способом и с теми же цифрами, что в ведомости отделки (способ счёта — в общих указаниях); объём краски к заказу, фасовка и материалы КМ — в спецификации отделочных материалов.
5. Колерная карта на 2 листах: обозначения повторены на каждом, схема квартиры и палитра — на первом, перечень выкрасов — на последнем.

| | | | | | |
|---|---|---|---|---|---|
| | | | | | Проект: Четырёхкомнатная квартира |
| | Лист | № док. | Подпись | Дата | |
| Дизайнер | Кырлан А.С. | | | 05.10.26 | Колерная карта |
| | | | | | Стадия: П; Лист: 11; Листов: 111 |

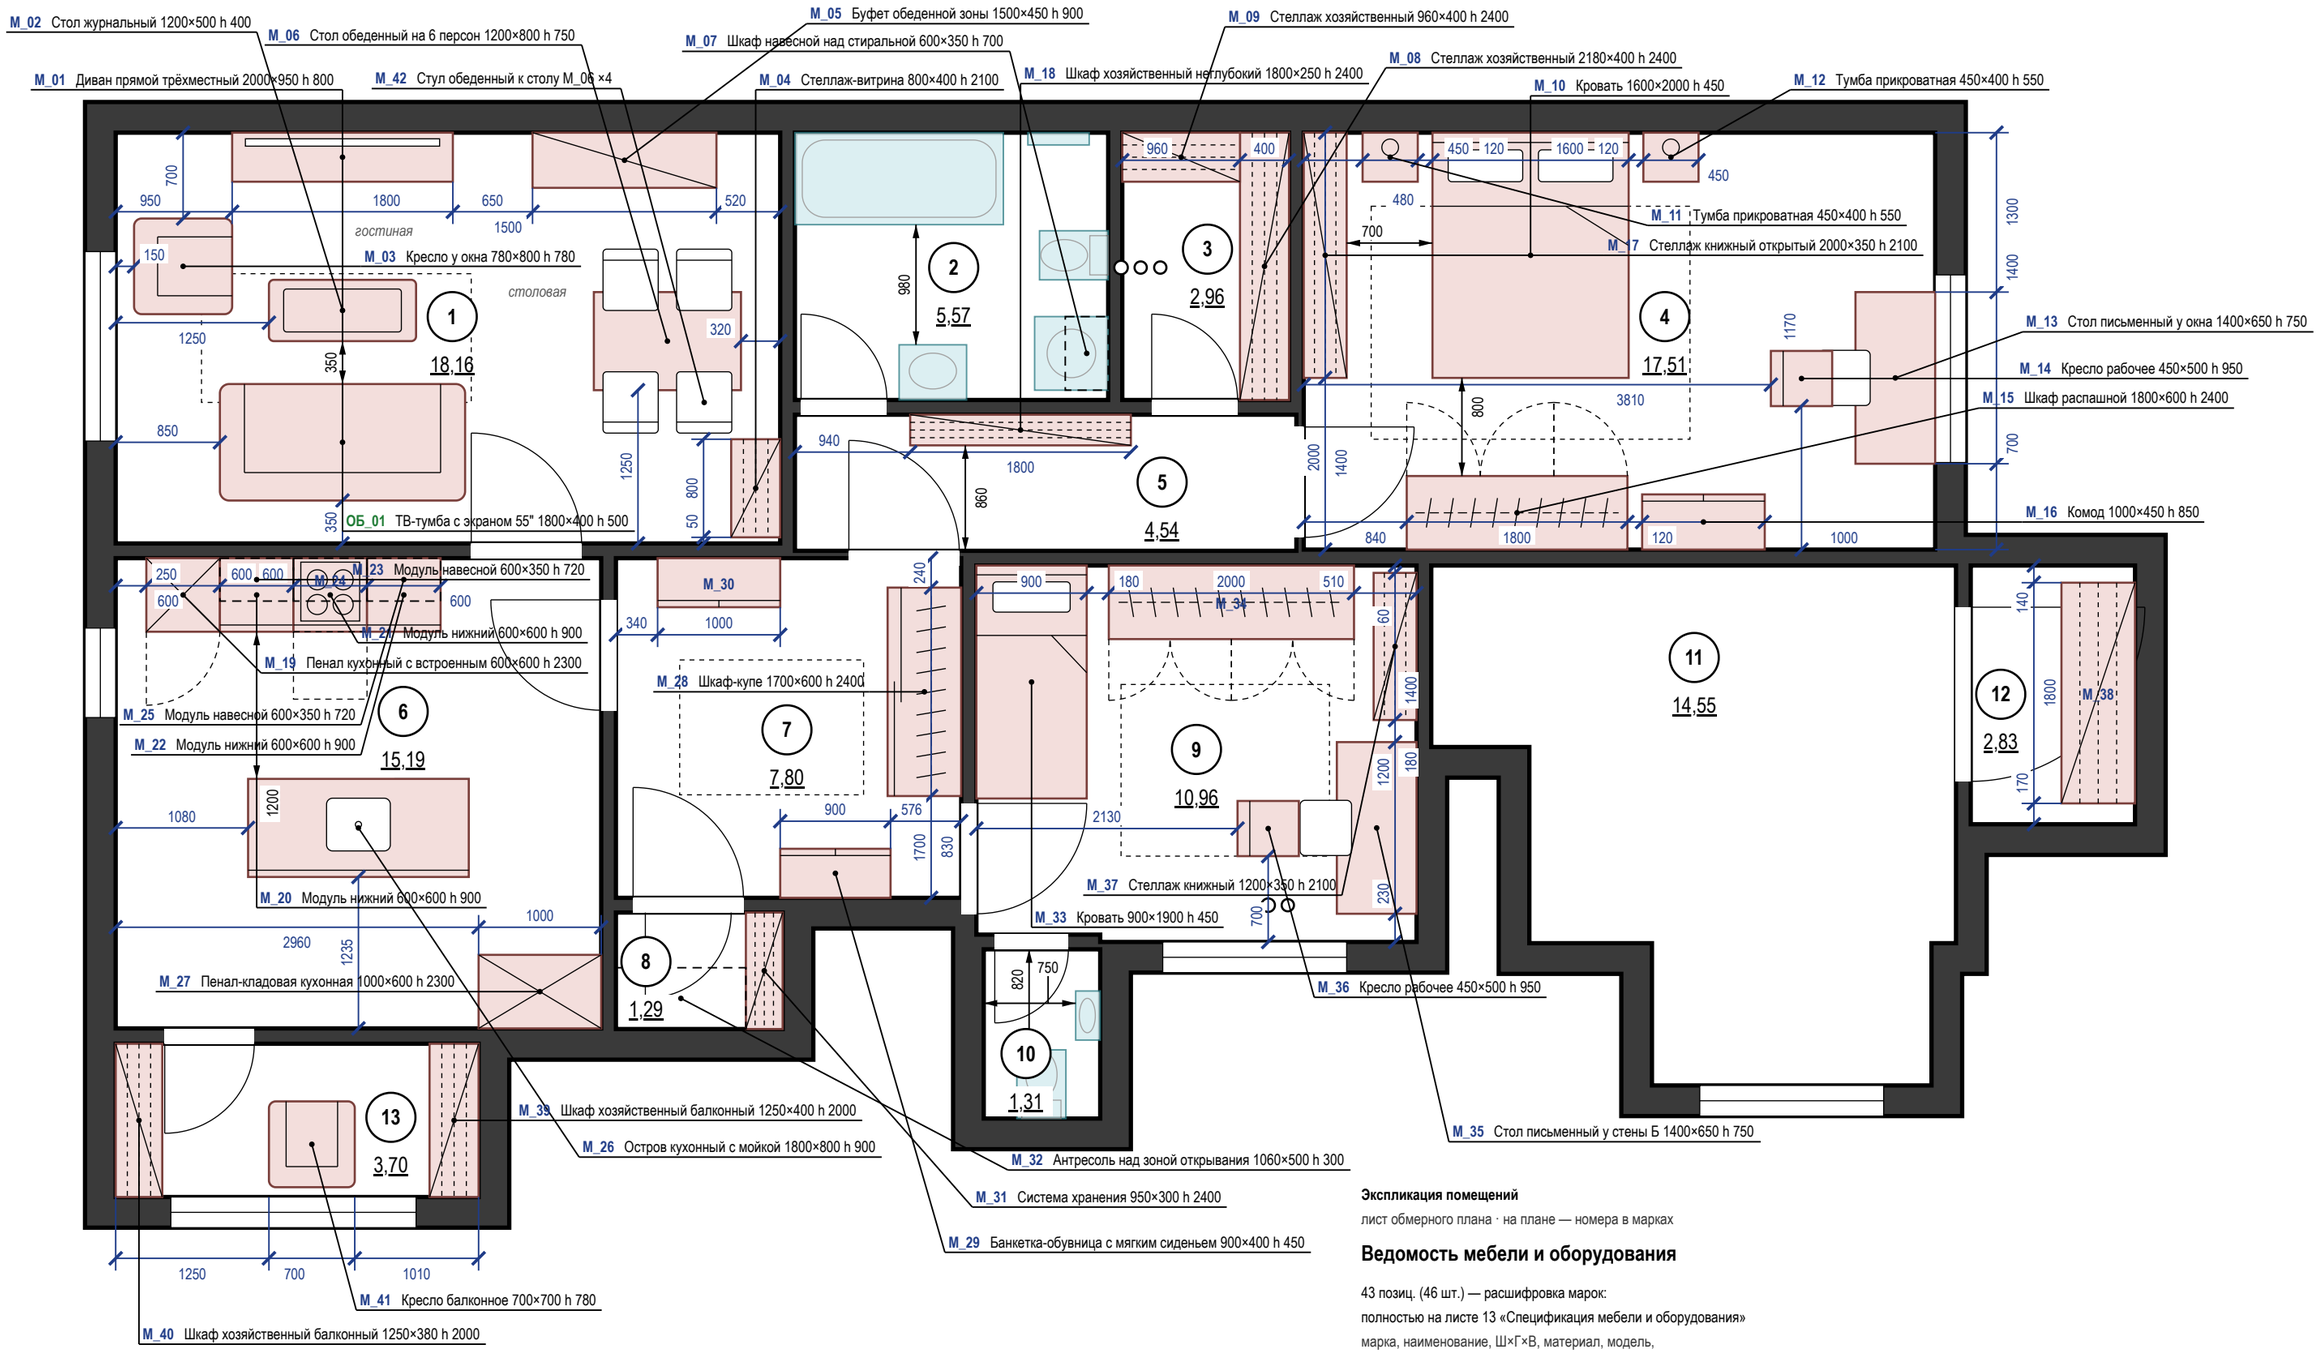


**Экспликация помещений**

лист обмерного плана · на плане — номера в марках

## Ведомость мебели и оборудования

43 позиц. (46 шт.) — расшифровка марок:
полностью на листе 13 «Спецификация мебели и оборудования»
марка, наименование, Ш×Г×В, материал, модель,
допуск замены. Марки на плане — по ней.

## Примечания

1. Размеры — в мм от чистовых поверхностей стен; размеры мебели уточнить после отделочных работ; общие указания — лист 2.
2. Отступ от стены, на плане не образмерен: М_41 — 80 мм.
3. Стулья обеденной группы (М_42 — 4 шт.) показаны в рабочем положении, задвинутыми под столешницу на 150 мм.

| | | | | | Проект: Четырёхкомнатная квартира | | | |
|---|---|---|---|---|---|---|---|---|
| | Лист | № док. | Подпись | Дата | План размещения мебели и оборудования | Стадия | Лист | Листов |
| Дизайнер | Кырлан А.С. | | | 05.10.26 | | П | 12 | 111 |

выпуск 05.10.2026 № 05166c8858 · стр. 12 из 111

| Поз. | Наименование и техническая характеристика | Тип, марка, обозначение документа, опросного листа | Код продукции | Поставщик | Ед. измерения | Кол. | Масса 1 ед., кг | Примечание |
|---|---|---|---|---|---|---|---|---|
| | **Мебель встроенная и корпусная (изготовление по чертежам мебельщика)** | | | | | | | |
| M_08 | Стеллаж хозяйственный, 6 полок; дерево — дуб натуральный; Ш×Г×В 2180×400×2400 мм | | | изготовление на заказ | шт. | 1 | | пом. 3; крепление к стене |
| M_09 | Стеллаж хозяйственный, 6 полок; дерево — дуб натуральный; Ш×Г×В 960×400×2400 мм | | | изготовление на заказ | шт. | 1 | | пом. 3; крепление к стене |
| M_15 | Шкаф распашной, 3 секции; дерево — дуб натуральный; Ш×Г×В 1800×600×2400 мм | | | изготовление на заказ | шт. | 1 | | пом. 4; крепление к стене |
| M_18 | Шкаф хозяйственный неглубокий; дерево — дуб натуральный; Ш×Г×В 1800×250×2400 мм | | | изготовление на заказ | шт. | 1 | | пом. 5; крепление к стене |
| M_19 | Пенал кухонный с встроенным холодильником; дерево — дуб натуральный, металл — чёрный матовый; Ш×Г×В 600×600×2300 мм | | | изготовление на заказ | шт. | 1 | | пом. 6; крепление к стене |
| M_20 | Модуль нижний, ящики; металл — чёрный матовый; Ш×Г×В 600×600×900 мм | | | изготовление на заказ | шт. | 1 | | пом. 6 |
| M_21 | Модуль нижний: варочная панель и духовой шкаф; металл — чёрный матовый; Ш×Г×В 600×600×900 мм | | | изготовление на заказ | шт. | 1 | | пом. 6 |
| M_22 | Модуль нижний, ящики и бутылочница; металл — чёрный матовый; Ш×Г×В 600×600×900 мм | | | изготовление на заказ | шт. | 1 | | пом. 6 |
| M_23 | Модуль навесной, 2 секции; металл — чёрный матовый; Ш×Г×В 600×350×720 мм | | | изготовление на заказ | шт. | 1 | | пом. 6 |
| M_24 | Вытяжка встраиваемая в шкаф; металл — чёрный матовый; Ш×Г×В 600×350×600 мм | | | изготовление на заказ | шт. | 1 | | пом. 6 |
| M_25 | Модуль навесной, 2 секции; металл — чёрный матовый; Ш×Г×В 600×350×720 мм | | | изготовление на заказ | шт. | 1 | | пом. 6 |
| M_26 | Остров кухонный с мойкой и посудомоечной машиной; дерево — дуб натуральный, металл — чёрный матовый; Ш×Г×В 1800×800×900 мм | | | изготовление на заказ | шт. | 1 | | пом. 6 |
| M_27 | Пенал-кладовая кухонная; дерево — дуб натуральный, металл — чёрный матовый; Ш×Г×В 1000×600×2300 мм | | | изготовление на заказ | шт. | 1 | | пом. 6; крепление к стене |
| M_28 | Шкаф-купе, 3 двери; дерево — дуб натуральный, металл — чёрный матовый; Ш×Г×В 1700×600×2400 мм | | | изготовление на заказ | шт. | 1 | | пом. 7; крепление к стене |
| M_31 | Система хранения: штанга, полки, ящики; дерево — дуб натуральный; Ш×Г×В 950×300×2400 мм | | | изготовление на заказ | шт. | 1 | | пом. 8; крепление к стене |
| M_32 | Антресоль над зоной открывания двери; дерево — дуб натуральный; Ш×Г×В 1060×500×300 мм | | | изготовление на заказ | шт. | 1 | | пом. 8; крепление к стене |
| M_34 | Шкаф распашной, 4 секции; дерево — дуб натуральный; Ш×Г×В 2000×600×2400 мм | | | изготовление на заказ | шт. | 1 | | пом. 9; крепление к стене |
| M_38 | Система хранения торцевая: штанги, полки; дерево — дуб натуральный; Ш×Г×В 1800×600×2400 мм | | | изготовление на заказ | шт. | 1 | | пом. 12; крепление к стене |
| M_39 | Шкаф хозяйственный балконный; дерево — дуб натуральный; Ш×Г×В 1250×400×2000 мм | | | изготовление на заказ | шт. | 1 | | пом. 13; крепление к стене |
| M_40 | Шкаф хозяйственный балконный; дерево — дуб натуральный; Ш×Г×В 1250×380×2000 мм | | | изготовление на заказ | шт. | 1 | | пом. 13; крепление к стене |
| | **Мебель покупная** | | | | | | | |
| M_01 | Диван прямой трёхместный; обивка букле; Ш×Г×В 2000×950×800 мм | диван прямой, глубокая посадка, съёмные чехлы | | аналог по характеристикам | шт. | 1 | | пом. 1; допуск замены Ш 1900–2100, Г ≤ 1000 |
| M_02 | Стол журнальный; дерево — дуб натуральный; Ш×Г×В 1200×500×400 мм | стол журнальный прямоугольный | | аналог по характеристикам | шт. | 1 | | пом. 1; допуск замены Ш 1100–1300 |
| M_03 | Кресло у окна; обивка — ткань, цвет Tikkurila V486; Ш×Г×В 780×800×780 мм | кресло мягкое на деревянных ножках | | аналог по характеристикам | шт. | 1 | | пом. 1; допуск замены Ш 750–850, В ≤ 790 (не выше подоконника) |
| M_04 | Стеллаж-витрина; дерево — дуб натуральный, металл — латунь; Ш×Г×В 800×400×2100 мм | стеллаж открытый, 5 полок | | аналог по характеристикам | шт. | 1 | | пом. 1; крепление к стене; допуск замены Ш 750–850 |
| M_05 | Буфет обеденной зоны; дерево — дуб натуральный, металл — латунь; Ш×Г×В 1500×450×900 мм | буфет 3-дверный | | аналог по характеристикам | шт. | 1 | | пом. 1; крепление к стене; допуск замены Ш 1400–1600, Г ≤ 470 |

## Примечания

1. Позиции мебели совпадают с марками на плане расстановки; размеры Ш×Г×В — Ш вдоль стены, Г от стены.
2. Встроенная и корпусная мебель изготавливается по чертежам мебельщика после контрольного обмера; графы «Тип, марка» и «Код продукции» для неё не заполняются (ГОСТ 21.110-2013).
3. Покупные изделия — аналог по характеристикам: заменять только на изделия не больше указанного габарита и того же материала и цвета.
4. Материал и цвет, не указанные в данных изделия, приняты по концепции: тон дерева — по полу, обивка — по вторичному цвету палитры; образцы согласовать до заказа.
5. Масса 1 ед. для изделий до 25 кг не указывается. Техника — по монтажным схемам изготовителя; выводы — по листам ЭОМ и ВК.

| | | | | | |
|---|---|---|---|---|---|
| | | | | | Проект: Четырёхкомнатная квартира |
| | Лист | № док. | Подпись | Дата | Спецификация мебели и оборудования |
| Дизайнер | Кырлан А.С. | | | 05.10.26 | |

| Стадия | Лист | Листов |
|---|---|---|
| П | 13 | 111 |

выпуск 05.10.2026 № 05166c8858 · стр. 13 из 111

| Поз. | Наименование и техническая характеристика | Тип, марка, обозначение документа, опросного листа | Код продукции | Поставщик | Ед. измерения | Кол. | Масса 1 ед., кг | Примечание |
|---|---|---|---|---|---|---|---|---|
| M_06 | Стол обеденный на 6 персон; дерево — дуб натуральный; Ш×Г×В 1200×800×750 мм | стол обеденный прямоугольный, раскладной до 1800 | | аналог по характеристикам | шт. | 1 | | пом. 1; допуск замены Ш 1200–1400 в сложенном виде, Г 800–900 |
| M_42 | Стул обеденный к столу M_06; обивка — ткань, цвет Tikkurila V486; каркас — дуб натуральный; Ш×Г×В 450×500×820 мм | | | аналог по характеристикам | шт. | 4 | | пом. 1; замена ≤ габарита |
| ОБ_01 | ТВ-тумба с экраном 55" дерево — дуб натуральный, металл — латунь; Ш×Г×В 1800×400×500 мм | тумба ТВ подвесная, 3 ящика | | аналог по характеристикам | шт. | 1 | | пом. 1; допуск замены Ш 1700–1900, Г ≤ 450 |
| M_07 | Шкаф навесной над стиральной машиной; дерево — дуб натуральный, металл — хром; Ш×Г×В 600×350×700 мм | | | аналог по характеристикам | шт. | 1 | | пом. 2; крепление к стене; замена ≤ габарита |
| M_10 | Кровать 1600×2000; мягкое изголовье, обивка — ткань, цвет Tikkurila V486; Ш×Г×В 1600×2000×450 мм | кровать с мягким изголовьем | | аналог по характеристикам | шт. | 1 | | пом. 4; допуск замены Ш 1600, Д 2000–2050 |
| M_11, M_12 | Тумба прикроватная; дерево — дуб натуральный; Ш×Г×В 450×400×550 мм | тумба прикроватная, 2 ящика | | аналог по характеристикам | шт. | 2 | | пом. 4; допуск замены Ш 400–500 |
| M_13 | Стол письменный у окна; дерево — дуб натуральный, металл — чёрный матовый; Ш×Г×В 1400×650×750 мм | стол письменный с тумбой | | аналог по характеристикам | шт. | 1 | | пом. 4; допуск замены Ш 1300–1500, Г 600–700 |
| M_14, M_36 | Кресло рабочее; металл — чёрный матовый; Ш×Г×В 450×500×950 мм | кресло рабочее на роликах | | аналог по характеристикам | шт. | 2 | | пом. 4, 9; допуск замены Ш 480–560 |
| M_16 | Комод, 4 ящика; дерево — дуб натуральный; Ш×Г×В 1000×450×850 мм | комод 4 ящика | | аналог по характеристикам | шт. | 1 | | пом. 4; крепление к стене; допуск замены Ш 950–1100 |
| M_17 | Стеллаж книжный открытый; дерево — дуб натуральный; Ш×Г×В 2000×350×2100 мм | | | аналог по характеристикам | шт. | 1 | | пом. 4; крепление к стене; замена ≤ габарита |
| M_29 | Банкетка-обувница с мягким сиденьем; дерево — дуб натуральный; Ш×Г×В 900×400×450 мм | банкетка-обувница | | аналог по характеристикам | шт. | 1 | | пом. 7; допуск замены Ш 800–950 |
| M_30 | Консоль прихожей, 3 ящика; дерево — дуб натуральный, металл — чёрный матовый; Ш×Г×В 1000×400×850 мм | консоль-комод | | аналог по характеристикам | шт. | 1 | | пом. 7; крепление к стене; допуск замены Ш 950–1100 |
| M_33 | Кровать 900×1900; мягкое изголовье, обивка — ткань, цвет Tikkurila V486; Ш×Г×В 900×1900×450 мм | кровать односпальная с мягким изголовьем | | аналог по характеристикам | шт. | 1 | | пом. 9; допуск замены Ш 900, Д 1900–1950 |
| M_35 | Стол письменный у стены Б, рядом с окном стены В: свет боковой; дерево — дуб натуральный, металл — чёрный матовый; Ш×Г×В 1400×650×750 мм | стол письменный с тумбой | | аналог по характеристикам | шт. | 1 | | пом. 9; допуск замены Ш 1300–1500, Г 600–700 |
| M_37 | Стеллаж книжный; дерево — дуб натуральный; Ш×Г×В 1200×350×2100 мм | | | аналог по характеристикам | шт. | 1 | | пом. 9; крепление к стене; замена ≤ габарита |
| M_41 | Кресло балконное; металл — чёрный матовый; Ш×Г×В 700×700×780 мм | кресло на металлическом каркасе | | аналог по характеристикам | шт. | 1 | | пом. 13; допуск замены Ш 650–750, В ≤ 850 (не выше подоконника) |
| | **Техника встраиваемая и бытовая, светильники под розетки** | | | | | | | |
| | Стиральная машина встраиваемая, у M_07 | | | аналог по характеристикам | шт. | 1 | | пом. 2; по схеме изготовителя |
| | Холодильник встраиваемый, в модуле M_19 | | | аналог по характеристикам | шт. | 1 | | пом. 6; по схеме изготовителя |
| | Духовой шкаф встраиваемый, в модуле M_21 | | | аналог по характеристикам | шт. | 1 | | пом. 6; по схеме изготовителя |
| | Варочная панель встраиваемая, электрическая, в модуле M_21 | | | аналог по характеристикам | шт. | 1 | | пом. 6; по схеме изготовителя |
| | Вытяжка встраиваемая, в модуле M_24 | | | аналог по характеристикам | шт. | 1 | | пом. 6; по схеме изготовителя |
| | Посудомоечная машина встраиваемая, в модуле M_26; ниша 600 мм | | | аналог по характеристикам | шт. | 1 | | пом. 6; по схеме изготовителя |

| | | | | | | |
|---|---|---|---|---|---|---|
| | | | | | Проект: Четырёхкомнатная квартира | |
| | Лист | № док. | Подпись | Дата | | |
| Дизайнер | Кырлан А.С. | | | 05.10.26 | Спецификация мебели и оборудования (продолжение) | Стадия: П; Лист: 14; Листов: 111 |

| Поз. | Наименование и техническая характеристика | Тип, марка, обозначение документа, опросного листа | Код продукции | Поставщик | Ед. измерения | Кол. | Масса 1 ед., кг | Примечание |
|---|---|---|---|---|---|---|---|---|
| | Торшер, у поз. M_01; абажур — ткань или опаловое стекло; лампа 2700 K | | | аналог по характеристикам | шт. | 1 | | пом. 1; розетка P3 (ЭОМ) |
| | **Текстиль** | | | | | | | |
| T1 | Портьеры-волна, два полотна; лён 100 %; цвет Tikkurila V486; карниз 2150 мм, высота 2690 мм, сборка 2 | | | аналог по характеристикам | шт. | 2 | | пом. 1 |
| T2 | Тюль-вуаль, одно полотно; полиэстер 100 %; цвет Tikkurila F497; карниз 2150 мм, высота 2690 мм, сборка 2,5 | | | аналог по характеристикам | шт. | 1 | | пом. 1 |
| T3 | Ковёр мягкой группы; шерсть 100 %; цвет NCS S 3005-Y20R; 2200×1050 мм | | | аналог по характеристикам | шт. | 1 | | пом. 1; с подложкой |
| T4 | Подушки декоративные на диван; лён 100 %; цвет Tikkurila H487 | | | аналог по характеристикам | шт. | 3 | | пом. 1 |
| T5 | Подушки декоративные на диван, акцент; хлопковый бархат 100 %; цвет Tikkurila L481 | | | аналог по характеристикам | шт. | 2 | | пом. 1 |
| T6 | Плед на диван; шерсть мериноса 100 %; цвет Tikkurila L481 | | | аналог по характеристикам | шт. | 1 | | пом. 1 |
| T7 | Раннер на обеденный стол; лён 100 %; цвет Tikkurila J484 | | | аналог по характеристикам | шт. | 1 | | пом. 1 |
| T8 | Портьеры стационарные, два полотна; лён 55 %, хлопок 45 %; цвет Tikkurila V484; карниз 2140 мм, высота 2690 мм, сборка 2 | | | аналог по характеристикам | шт. | 2 | | пом. 4 |
| T9 | Римская штора блэкаут: окно закрывает она, стол M_13 у окна не мешает; хлопок 100 %, подкладка полиэстер; цвет Tikkurila H487; карниз 1650 мм, высота 1900 мм | | | аналог по характеристикам | шт. | 1 | | пом. 4 |
| T10 | Ковёр у кровати; шерсть 80 %, хлопок 20 %; цвет Tikkurila H487; 2600×1900 мм | | | аналог по характеристикам | шт. | 1 | | пом. 4; с подложкой |
| T11 | Подушки декоративные на кровать; лён 100 %; цвет Tikkurila H487 | | | аналог по характеристикам | шт. | 2 | | пом. 4 |
| T12 | Подушка декоративная, акцент; хлопковый бархат 100 %; цвет NCS S 5010-B10G | | | аналог по характеристикам | шт. | 1 | | пом. 4 |
| T13 | Плед на кровать; хлопок 100 %; цвет NCS S 5010-B10G | | | аналог по характеристикам | шт. | 1 | | пом. 4 |
| T14 | Рулонная штора кассетная, ткань димаут; полиэстер 100 %; цвет Tikkurila J484; карниз 890 мм, высота 1900 мм | | | аналог по характеристикам | шт. | 1 | | пом. 6 |
| T15 | Ковёр прихожей, низкий ворс; шерсть 80 %, полиамид 20 %; цвет NCS S 3005-Y20R; 1500×1100 мм | | | аналог по характеристикам | шт. | 1 | | пом. 7; с подложкой |
| T16 | Портьеры стационарные, два полотна, до подоконника: радиатор под окном открыт; лён 55 %, хлопок 45 %; цвет Tikkurila V484; карниз 1800 мм, высота 1930 мм, сборка 2 | | | аналог по характеристикам | шт. | 2 | | пом. 9 |
| T17 | Римская штора блэкаут: закрывает проём целиком, радиатор под окном не задевает; хлопок 100 %, подкладка полиэстер; цвет Tikkurila H487; карниз 1620 мм, высота 1900 мм | | | аналог по характеристикам | шт. | 1 | | пом. 9 |
| T18 | Ковёр игровой зоны; шерсть 100 %; цвет NCS S 3005-Y20R; 1700×1400 мм | | | аналог по характеристикам | шт. | 1 | | пом. 9; с подложкой |
| T19 | Подушки декоративные на кровать; лён 100 %; цвет Tikkurila H487 | | | аналог по характеристикам | шт. | 2 | | пом. 9 |
| T20 | Подушка декоративная, акцент; шерсть 60 %, полиэстер 40 %; цвет Farrow & Ball No. 47 | | | аналог по характеристикам | шт. | 1 | | пом. 9 |
| T21 | Плед на кровать; хлопок 100 %; цвет Farrow & Ball No. 47 | | | аналог по характеристикам | шт. | 1 | | пом. 9 |
| T22 | Рулонная штора кассетная, солнцезащитная; полиэстер 100 %; цвет Tikkurila V486; карниз 2140 мм, высота 1700 мм | | | аналог по характеристикам | шт. | 1 | | пом. 13 |
| T23 | Плед на кресло M_41; шерсть 100 %; цвет Tikkurila V484 | | | аналог по характеристикам | шт. | 1 | | пом. 13 |
| | **Декор** | | | | | | | |
| ДК1 | Картина над диваном: крупная абстракция, холст, тонкая рама; 1400×900 мм; низ на 1000 мм от пола | | | аналог по характеристикам | шт. | 1 | 6 | пом. 1; крепление: планка на дюбелях, 4 точки |
| ДК2 | Зеркало над буфетом, рама шпон дуба; 1000×800 мм; низ на 1100 мм от пола | | | аналог по характеристикам | шт. | 1 | 12 | пом. 1; крепление: анкер химический, 4 точки |

| | | | | | | |
|---|---|---|---|---|---|---|
| | | | | | Проект: Четырёхкомнатная квартира | |
| | Лист | № док. | Подпись | Дата | | |
| Дизайнер | Кырлан А.С. | | | 05.10.26 | Спецификация мебели и оборудования (продолжение) | Стадия: П; Лист: 15; Листов: 111 |

| Поз. | Наименование и техническая характеристика | Тип, марка, обозначение документа, опросного листа | Код продукции | Поставщик | Ед. измерения | Кол. | Масса 1 ед., кг | Примечание |
|---|---|---|---|---|---|---|---|---|
| ДК3 | Фикус лировидный в кашпо Ø400; 450×450 мм | | | аналог по характеристикам | шт. | 1 | | пом. 1 |
| ДК4 | Зеркало над раковиной C_03, влагостойкое; 600×800 мм; низ на 1100 мм от пола | | | аналог по характеристикам | шт. | 1 | 5 | пом. 2; крепление: зеркалодержатели, 4 точки |
| ДК5 | Картина над изголовьем: графика, паспарту, рама; 1100×700 мм; низ на 1300 мм от пола | | | аналог по характеристикам | шт. | 1 | 4 | пом. 4; крепление: две петли на дюбелях |
| ДК6 | Зеркало над комодом M_16; 700×900 мм; низ на 1050 мм от пола | | | аналог по характеристикам | шт. | 1 | 8 | пом. 4; крепление: анкер химический, 4 точки |
| ДК7 | Хлорофитум хохлатый в напольном кашпо Ø380; 420×420 мм | | | аналог по характеристикам | шт. | 1 | | пом. 4 |
| ДК8 | Часы настенные Ø400; 400×400 мм; центр на 1550 мм от пола | | | аналог по характеристикам | шт. | 1 | 2 | пом. 6; крепление: дюбель с крюком, 1 точка |
| ДК9 | Хлорофитум хохлатый на подоконнике (отм. +0,800); 300×200 мм; низ на 800 мм от пола | | | аналог по характеристикам | шт. | 1 | | пом. 6 |
| ДК10 | Зеркало над консолью M_30; 700×1000 мм; низ на 1050 мм от пола | | | аналог по характеристикам | шт. | 1 | 9 | пом. 7; крепление: анкер химический, 4 точки |
| ДК11 | Замиокулькас в напольном кашпо Ø360; 400×400 мм | | | аналог по характеристикам | шт. | 1 | | пом. 7 |
| ДК12 | Картина над изголовьем: графика, паспарту, рама; 600×800 мм; низ на 1200 мм от пола | | | аналог по характеристикам | шт. | 1 | 3 | пом. 9; крепление: две петли на дюбелях |
| ДК13 | Постер в раме, левый (группа «постеры»); 400×500 мм; низ на 1250 мм от пола | | | аналог по характеристикам | шт. | 1 | 2 | пом. 9; крепление: петля на дюбеле |
| ДК14 | Постер в раме, средний (группа «постеры»); 400×500 мм; низ на 1250 мм от пола | | | аналог по характеристикам | шт. | 1 | 2 | пом. 9; крепление: петля на дюбеле |
| ДК15 | Постер в раме, правый (группа «постеры»); 400×500 мм; низ на 1250 мм от пола | | | аналог по характеристикам | шт. | 1 | 2 | пом. 9; крепление: петля на дюбеле |
| ДК16 | Спатифиллум в напольном кашпо Ø360; 400×400 мм | | | аналог по характеристикам | шт. | 1 | | пом. 9 |
| ДК17 | Зеркало над раковиной C_07, влагостойкое; 500×700 мм; низ на 1150 мм от пола | | | аналог по характеристикам | шт. | 1 | 4 | пом. 10; крепление: зеркалодержатели, 4 точки |
| ДК20 | Картина: тёмная лиловая абстракция, холст, тонкая рама; 800×600 мм; низ на 1300 мм от пола | | | аналог по характеристикам | шт. | 1 | 4 | пом. 11; крепление: планка на дюбелях, 2 точки |
| ДК21 | Ваза напольная, керамика матовая; 300×300 мм | | | аналог по характеристикам | шт. | 1 | | пом. 11 |
| ДК18 | Зеркало ростовое 500×1600; 500×1600 мм; низ на 250 мм от пола | | | аналог по характеристикам | шт. | 1 | 12 | пом. 12; крепление: анкер химический, 4 точки + опора снизу |
| ДК19 | Лавр благородный в напольном кашпо Ø380; 400×400 мм | | | аналог по характеристикам | шт. | 1 | | пом. 13 |

| | | | | | | | | |
|---|---|---|---|---|---|---|---|---|
| | | | | | | Проект: Четырёхкомнатная квартира | | |
| | Лист | № док. | Подпись | Дата | | | | |
| Дизайнер | Кырлан А.С. | | | 05.10.26 | Спецификация мебели и оборудования (продолжение) | Стадия | Лист | Листов |
| | | | | | | П | 16 | 111 |

выпуск 05.10.2026 № 05166c8858 · стр. 16 из 111

## Ведомость изделий

| Марка | Наименование | Пом. | Ш×Г×В, мм | Корпус | Фасад | Кромка, мм скр./вид. | Кол. |
|---|---|---|---|---|---|---|---|
| M_07 | Система хранения | 2 | 600×350×700 | ЛДСП 16 | без фасадов; ящики — МДФ 18, эмаль матовая | 0,4 / 2 | 1 |
| M_08 | Система хранения | 3 | 2180×400×2400 | ЛДСП 16 | без фасадов; ящики — МДФ 18, эмаль матовая | 0,4 / 2 | 1 |
| M_09 | Система хранения | 3 | 960×400×2400 | ЛДСП 16 | без фасадов; ящики — МДФ 18, эмаль матовая | 0,4 / 2 | 1 |
| M_15 | Шкаф распашной | 4 | 1800×600×2400 | ЛДСП 16 | МДФ 18, эмаль матовая | 0,4 / 2 | 1 |
| M_17 | Система хранения | 4 | 2000×350×2100 | ЛДСП 16 | без фасадов; ящики — МДФ 18, эмаль матовая | 0,4 / 2 | 1 |
| M_18 | Система хранения | 5 | 1800×250×2400 | ЛДСП 16 | МДФ 18, эмаль матовая | 0,4 / 2 | 1 |
| M_28 | Шкаф-купе | 7 | 1700×600×2400 | ЛДСП 16 | рифлёные панели МДФ в алюминиевом профиле | 0,4 / 2 | 1 |
| M_31 | Система хранения | 8 | 950×300×2400 | ЛДСП 16 | без фасадов; ящики — МДФ 18, эмаль матовая | 0,4 / 2 | 1 |
| M_32 | Система хранения | 8 | 1060×500×300 | ЛДСП 16 | без фасадов; ящики — МДФ 18, эмаль матовая | 0,4 / 2 | 1 |
| M_34 | Шкаф распашной | 9 | 2000×600×2400 | ЛДСП 16 | МДФ 18, эмаль матовая | 0,4 / 2 | 1 |
| M_38 | Система хранения | 12 | 1800×600×2400 | ЛДСП 16 | без фасадов; ящики — МДФ 18, эмаль матовая | 0,4 / 2 | 1 |
| M_39 | Система хранения | 13 | 1250×400×2000 | ЛДСП 16 | без фасадов; ящики — МДФ 18, эмаль матовая | 0,4 / 2 | 1 |
| M_40 | Система хранения | 13 | 1250×380×2000 | ЛДСП 16 | без фасадов; ящики — МДФ 18, эмаль матовая | 0,4 / 2 | 1 |
| M_19 | Пенал: холодильник встр. | 6 | 600×600×2300 | ЛДСП 16 | МДФ 18, эмаль матовая | 0,4 / 2 | 1 |
| M_20 | Модуль нижний: ящики | 6 | 600×600×900 | ЛДСП 16 | МДФ 18, эмаль матовая | 0,4 / 2 | 1 |
| M_23 | Модуль навесной: полки | 6 | 600×350×720 | ЛДСП 16 | МДФ 18, эмаль матовая | 0,4 / 2 | 1 |
| M_21 | Модуль нижний: духовой шкаф, варочная | 6 | 600×600×900 | ЛДСП 16 | МДФ 18, эмаль матовая | 0,4 / 2 | 1 |
| M_24 | Модуль навесной: полки | 6 | 600×350×600 | ЛДСП 16 | МДФ 18, эмаль матовая | 0,4 / 2 | 1 |
| M_22 | Модуль нижний: ящики | 6 | 600×600×900 | ЛДСП 16 | МДФ 18, эмаль матовая | 0,4 / 2 | 1 |
| M_25 | Модуль навесной: полки | 6 | 600×350×720 | ЛДСП 16 | МДФ 18, эмаль матовая | 0,4 / 2 | 1 |
| M_27 | Пенал: полки | 6 | 1000×600×2300 | ЛДСП 16 | МДФ 18, эмаль матовая | 0,4 / 2 | 1 |

## Ведомость встраиваемой техники

| Поз. | Прибор | Ниша, вырез, мм | Вентиляция | Питание | Схема |
|---|---|---|---|---|---|
| M_19 | Холодильник встраиваемый, ниша 1780 | ниша 1780 × 560 × 550 | решётка в цоколе, канал за корпусом, выход сверху | розетка над нишей или в соседнем модуле | по модели |
| M_21 | Духовой шкаф встраиваемый, 60 см | ниша 560 × 595, глубина ≥ 550 | зазор за шкафом, вырез в задней стенке | вывод кабеля под шкафом | по модели |
| M_21 | Варочная панель индукционная, 60 см | вырез в столешнице 560 × 490 | | вывод кабеля под модулем | по модели |
| M_21 | Вытяжка настенная, 60 см | низ ≥ 650 над панелью | воздуховод к вентканалу, короб до потолка | вывод кабеля в коробе | по модели |

## Ведомость фурнитуры


| № | Фурнитура | Тип, размер | Изделия | Кол. |
|---|---|---|---|---|
| 1 | Полкодержатель с фиксацией | ø5 мм | M_07, M_08, M_09, M_15, M_17, M_18, M_28, M_31, M_32, M_34, M_38, M_39, M_40, M_19, M_23, M_24, M_25, M_27 | 344 |
| 2 | Штанга выдвижная торцевая | L по глубине | M_07, M_08, M_09, M_17, M_32, M_39, M_40 | 11 |
| 3 | Анкер по основанию стены | по таблице крепежа | M_07, M_08, M_09, M_15, M_17, M_18, M_28, M_31, M_32, M_34, M_38, M_39, M_40, M_23, M_24, M_25 | 96 |
| 4 | Уголок крепления к стене от опрокидывания | стальной | M_07, M_08, M_09, M_15, M_17, M_18, M_28, M_31, M_32, M_34, M_38, M_39, M_40, M_19, M_27 | 30 |
| 5 | Опора регулируемая с цоколем на клипсах | ход 20 мм | M_08, M_09, M_15, M_17, M_18, M_28, M_31, M_34, M_38, M_39, M_40 | 80 |
| 6 | Петля накладная 110° с доводчиком | чашка 35 мм | M_15, M_18, M_34, M_19, M_23, M_24, M_25, M_27 | 96 |
| 7 | Штанга овальная 30×15, L = 876 | + 2 держателя | M_15 | 1 |
| 8 | Система дверей купе: профиль, направляющие, ролики | на 2 двери | M_28 | 1 |
| 9 | Ручка-профиль вертикальная | в цвет профиля | M_28 | 2 |
| 10 | Штанга овальная 30×15, L = 826 | + 2 держателя | M_28 | 1 |
| 11 | Полка для обуви выдвижная наклонная | ширина 826 | M_28 | 3 |
| 12 | Штанга овальная 30×15, L = 976 | + 2 держателя | M_34 | 1 |
| 13 | Штанга овальная 30×15, L = 579 | + 2 держателя | M_38 | 3 |
| 14 | Ручка-профиль | латунь матовая | M_19, M_20, M_23, M_21, M_24, M_22, M_25, M_27 | 18 |
| 15 | Опора кухонная регулируемая 100–120 мм | + клипса цоколя | M_19, M_20, M_21, M_22, M_27 | 22 |
| 16 | Направляющие полного выдвижения с доводчиком NL 500 | пара | M_20, M_21, M_22 | 7 |
| 17 | Навес регулируемый для навесного шкафа | пара на секцию | M_23, M_24, M_25 | 3 |
| 18 | Шина монтажная | L = 540 | M_23, M_24, M_25 | 3 |

## Примечания


1. Модели техники выбирает заказчик до изготовления мебели; ниши, вырезы и вентиляция — по монтажной схеме выбранной модели (условие гарантии), её номер вносится в ведомость.
2. Количество фурнитуры — по чертежам изделий; запас крепежа 5 %. Аналоги — по характеристикам (доводчик, нагрузка, ход).
3. Цвет корпусов, фасадов и профилей — по колерной карте проекта.

| | | | | | Проект: Четырёхкомнатная квартира | | | |
|---|---|---|---|---|---|---|---|---|
| | Лист | № док. | Подпись | Дата | Ведомости изделий, техники и фурнитуры | Стадия | Лист | Листов |
| Дизайнер | Кырлан А.С. | | | 05.10.26 | | П | 17 | 111 |


### Фрагмент 1. Ванная комната (пом. 2)

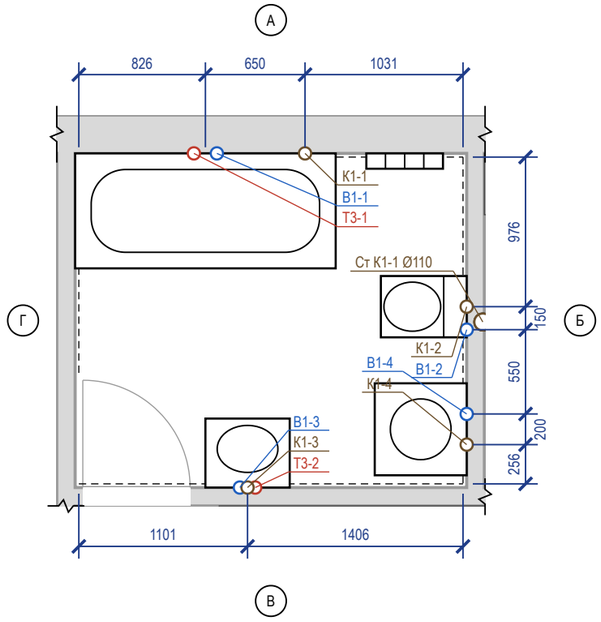


### Фрагмент 2. Кухня (пом. 6)

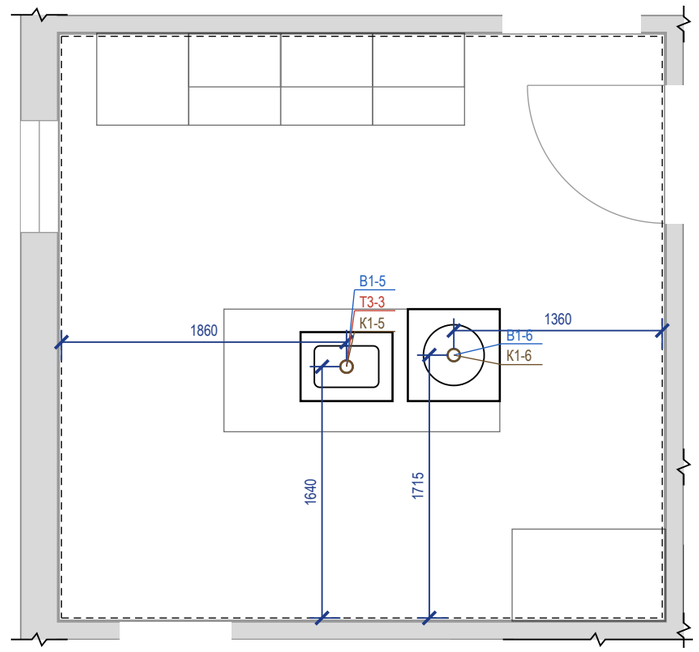


### Фрагмент 3. Санузел (пом. 10)

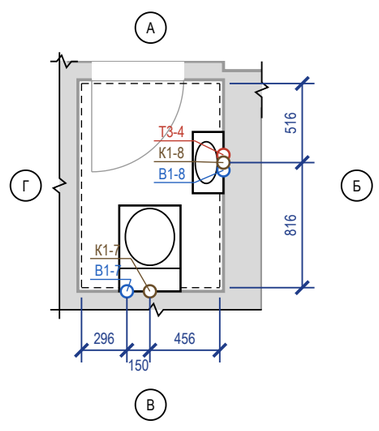


### Ведомость привязок выводов

| Код | Прибор | Ø | H, мм | Привязка от чист. стен, мм | Прим. |
|---|---|---|---|---|---|
| В1-1 | С_01 ванна | ½" | 800 | ст. А: 901 от Г | межос. 150 |
| Т3-1 | С_01 ванна | ½" | 800 | ст. А: 751 от Г | межос. 150 |
| К1-1 | С_01 ванна | Ø50 | 60 | ст. А: 1031 от Б | |
| В1-2 | С_02 унитаз подвесной | ½" | 250 | ст. Б: 1006 от В | в раме инсталляции |
| К1-2 | С_02 унитаз подвесной | Ø110 | 220 | ст. Б: 976 от А | |
| В1-3 | С_03 умывальник | ½" | 550 | ст. В: 1051 от Г | межос. 100 |
| Т3-2 | С_03 умывальник | ½" | 550 | ст. В: 1151 от Г | межос. 100 |
| К1-3 | С_03 умывальник | Ø40 | 450 | ст. В: 1101 от Г | |
| В1-4 | ОБ_02 стиральная машина | ½" | 700 | ст. Б: 456 от В | кран машины |
| К1-4 | ОБ_02 стиральная машина | Ø40 | 700 | ст. Б: 256 от В | |
| В1-5 | С_05 мойка кухонная | ½" | 600 | 1860 от Г; 1640 от В | межос. 100 |
| Т3-3 | С_05 мойка кухонная | ½" | 600 | 1860 от Г; 1640 от В | межос. 100 |
| К1-5 | С_05 мойка кухонная | Ø50 | 400 | 1860 от Г; 1640 от В | |
| В1-6 | ОБ_03 посудомоечная машина | ½" | 550 | 1360 от Б; 1715 от В | кран ПММ |
| К1-6 | ОБ_03 посудомоечная машина | Ø50 | 550 | 1360 от Б; 1715 от В | |
| В1-7 | С_06 унитаз подвесной | ½" | 250 | ст. В: 296 от Г | в раме инсталляции |
| К1-7 | С_06 унитаз подвесной | Ø110 | 220 | ст. В: 446 от Г | |
| В1-8 | С_07 умывальник | ½" | 550 | ст. Б: 566 от А | межос. 100 |
| Т3-4 | С_07 умывальник | ½" | 550 | ст. Б: 466 от А | межос. 100 |
| К1-8 | С_07 умывальник | Ø40 | 450 | ст. Б: 516 от А | |

### Условные обозначения

- вывод В1 (код — в ведомости привязок)
- вывод Т3 (код — в ведомости привязок)
- вывод К1 (код — в ведомости привязок)
- сантехприбор по расстановке (габарит модели)
- чистовая поверхность стены (от неё привязки)
- стояк «Ст К1-N / Ст В1-N» (ГОСТ 21.601), Ø мм
- стояк Т3 не на обмере — принят в шахте рядом со Ст В1, сверить
- линия обрыва (граница фрагмента)
- А — обозначение стены А–Г (как на развёртках)

### Примечания


1. Привязки выводов даны от чистовых поверхностей стен (облицовка на сторону: ванная комната — 24 мм (штукатурка 10 + клей 5 + плитка 9); кухня — 20 мм (по данным); санузел — 24 мм (штукатурка 10 + клей 5 + плитка 9)); эти же грани — на развёртках и в раскладке плитки. Высоты — от чистого пола помещения.
2. До черновой разводки сверить по паспорту выбранного прибора (смеситель, инсталляция, сифон).
3. Горячая вода (Т3) — слева от холодной (В1), если смотреть на прибор. Допуск установки выводов: ±5 мм в группе, ±20 мм у отдельно стоящих.
4. Расчёт систем водоснабжения и канализации и подбор оборудования выполняет проектная организация; лист задаёт места и высоты выводов.
5. Ст Т3-2 на обмере не показаны: приняты рядом с Ст В1-2 (в МКД стоят группой); положение сверить на объекте до разметки.
6. Штриховая линия чистовой грани стены прерывается на длине полотна открытой двери, лежащего вдоль грани (линии не должны сливаться при печати); положение грани — по размерам, а не по штриху.

| | | | | | |
|---|---|---|---|---|---|
| | | | | | Проект: Четырёхкомнатная квартира |
| | Лист | № док. | Подпись | Дата | План выводов сантехники |
| Дизайнер | Кырлан А.С. | | | 05.10.26 | |


| Стадия | Лист | Листов |
|---|---|---|
| П | 18 | 111 |

выпуск 05.10.2026 № 05166c8858 · стр. 18 из 111


## План квартиры (М 1:400)

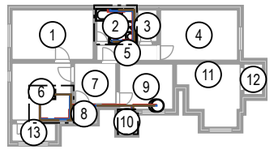



## Фр. 1. Ванная комната (М 1:40)

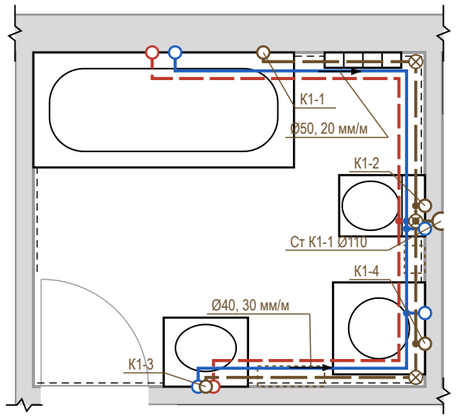


## Фр. 2. Кухня (М 1:40)

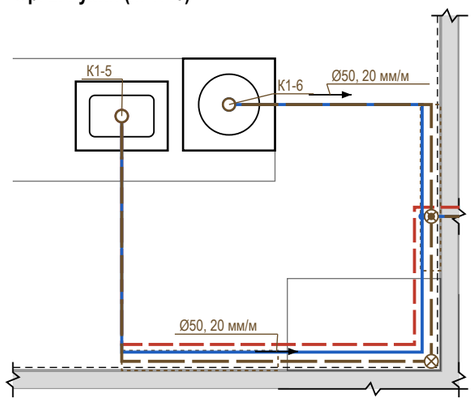


## Фр. 3. Санузел (М 1:40)

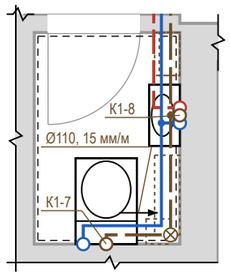


## Условные обозначения


- В1 — водопровод хозяйственно-питьевой (ХВС), PP-R Ø20
- Т3 — горячее водоснабжение, подача (ГВС), PP-R Ø20
- К1 — канализация бытовая
- направление уклона К1 / пола: Ø, мм на 1 м
- ⊗ ревизия (прочистка) К1 — доступ сохранить
- • тройник (ответвление к прибору)
- короб К1 над чистым полом (ГКЛВ под плитку)
- ○ вывод В1 (код — в ведомости привязок)
- ○ вывод Т3 (код — в ведомости привязок)
- ○ вывод К1 (код — в ведомости привязок)
- ▭ сантехприбор по расстановке (габарит модели)
- ◯ стояк «Ст К1-N / Ст В1-N» (ГОСТ 21.601), Ø мм
- ◌ стояк Т3 не на обмере — принят в шахте рядом со Ст В1, сверить
- ⌇ линия обрыва (граница фрагмента)
- ▭ граница фрагмента на плане (Фр. N)

## Профиль выпусков К1 (до врезки в стояк)

| Выпуск | Прибор | Ø | L, м | i, мм/м | Δh, мм | Прокладка, мм |
|---|---|---|---|---|---|---|
| К1-7 | С_06 унитаз подвесной | Ø110 | 3,60 | 15 | 54 | короб 200×140 |
| К1-2 | С_02 унитаз подвесной | Ø110 | 0,35 | 20 | 7 | над полом за приборами |
| К1-5 | С_05 мойка кухонная | Ø50 | 10,10 | 20 | 202 | короб 290×110 |
| К1-6 | ОБ_03 посудомоечная машина | Ø50 | 7,60 | 20 | 152 | короб 240×110 |
| К1-1 | С_01 ванна | Ø50 | 2,30 | 20 | 46 | в полу, стяжка ≥ 151 |
| К1-3 | С_03 умывальник | Ø40 | 2,65 | 30 | 80 | короб 150×110 |
| К1-8 | С_07 умывальник | Ø40 | 2,50 | 30 | 75 | короб 150×110 |
| К1-4 | ОБ_02 стиральная машина | Ø40 | 1,05 | 30 | 32 | в полу, стяжка ≥ 127 |

Короб h×b: h — от чистого пола, b — от чистовой стены. Стяжка 155 мм — лист полов.

## Узел ввода В1, Т3 (схема, без масштаба)

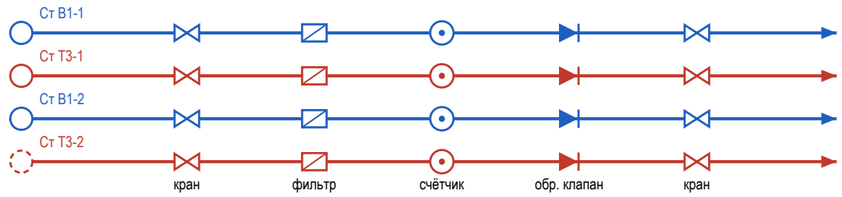


⊗ Ст К1-1, Ст К1-2: ревизия на стояке — люк в коробе

## Примечания

1. Трассы принципиальные, построены от стояков вдоль стен помещений; фактическое положение фиксируется исполнительной схемой с привязками (фото с рулеткой) до закрытия.
2. Уклон К1 не менее 1/d и не более 150 мм/м (СП 30.13330.2020, п. 19.1), приняты практические уклоны; поворот — двумя отводами 45°, ревизия после поворота, доступ сохранить. Стояк К1 в коробе — звукоизоляция стояка в коробе, без жёсткого контакта короба с трубой.
3. Решение по К1: стяжка 155 мм не укрывает трубы (нужно Ø + Δh + 45 мм) — выпуски идут над чистым полом вдоль стен: К1-2 — за приборами и в раме инсталляции; К1-7, К1-5, К1-6, К1-3, К1-8 — в коробе ГКЛВ под плитку (размеры в профиле). Короба — на развёртках; отметку низа врезки в стояк замерить до черновых работ.
4. На каждом вводе В1 и Т3 — кран шаровой, фильтр, счётчик, обратный клапан; доступ через люк не меньше 300×400. Водопровод — в штробе стен или в коробах; трубы испытать давлением до закрытия (акт скрытых работ).
5. Расчёт систем, диаметры магистралей и подбор оборудования выполняет проектная организация; врезка и перенос стояков — по согласованию с управляющей организацией. Арматуру и привязки сверить по паспортам приборов.
6. Ст Т3-2 на обмере не показаны: приняты рядом с Ст В1-2; положение сверить на объекте до разводки.
7. Штриховая линия чистовой грани стены прерывается на длине полотна открытой двери, лежащего вдоль грани (линии не должны сливаться при печати); положение грани — по размерам, а не по штриху.

| | | | | | | |
|---|---|---|---|---|---|---|
| | | | | | Проект: Четырёхкомнатная квартира | |
| | Лист | № док. | Подпись | Дата | | |
| Дизайнер | Кырлан А.С. | | | 05.10.26 | Схема разводки водопровода и канализации | Стадия: П; Лист: 19; Листов: 111 |


выпуск 05.10.2026 № 05166c8858 · стр. 19 из 111

| Поз. | Наименование и техническая характеристика | Тип, марка, обозначение документа | Код продукции | Поставщик | Ед. изм. | Кол. | Масса 1 ед., кг | Примечание |
|---|---|---|---|---|---|---|---|---|
| | Санитарные приборы | | | | | | | |
| 1 | Ванна акриловая 1700×750 мм, с каркасом, экраном и отверстием слив-перелив | аналог | | выбор заказчика | шт | 1 | 35 | С_01 |
| 2 | Унитаз подвесной безободковый, с сиденьем микролифт, крепёж и звукоизолирующая прокладка | аналог | | выбор заказчика | шт | 2 | | С_02, С_06 |
| 3 | Инсталляция для подвесного унитаза: рама высотой 1120 мм, бачок, клавиша смыва (ось клавиши 1050 мм от чистого пола) | аналог | | выбор заказчика | шт | 2 | | С_02, С_06; короб ГКЛВ |
| 4 | Умывальник подвесной 550×450 мм, с отверстием под смеситель и переливом | аналог | | выбор заказчика | шт | 1 | | С_03 |
| 5 | Умывальник подвесной 400×200 мм, с отверстием под смеситель и переливом | аналог | | выбор заказчика | шт | 1 | | С_07 |
| 6 | Мойка кухонная врезная 600×450 мм, с переливом | аналог | | с кухонной мебелью | шт | 1 | | С_05 |
| 7 | Полотенцесушитель электрический, IP44, с терморегулятором | аналог | | выбор заказчика | шт | 1 | | С_04 |
| | Смесители, сифоны и арматура приборов | | | | | | | |
| 8 | Смеситель для ванны настенный однорычажный, межосевое 150 мм, с душевым набором (лейка, шланг, держатель) | аналог | | выбор заказчика | шт | 1 | | С_01 |
| 9 | Смеситель для умывальника однорычажный, с донным клапаном | аналог | | выбор заказчика | шт | 2 | | С_03, С_07 |
| 10 | Смеситель кухонный однорычажный, высокий излив | аналог | | выбор заказчика | шт | 1 | | С_05 |
| 11 | Обвязка ванны слив-перелив Ø40/50 с сифоном | аналог | | выбор заказчика | шт | 1 | | С_01 |
| 12 | Сифон для умывальника бутылочный Ø32/40–50, с гофрой к выпуску | аналог | | выбор заказчика | шт | 2 | | С_03, С_07 |
| 13 | Сифон для мойки с отводом для ПММ Ø40/50 | аналог | | выбор заказчика | шт | 1 | | С_05 |
| 14 | Сифон для стиральной машины встраиваемый в стену Ø50, с обратным клапаном | аналог | | выбор заказчика | шт | 1 | | ОБ_02 |
| 15 | Кран угловой ½"×½" с гибкой подводкой 40 см (умывальники, мойка) | аналог | | выбор заказчика | шт | 6 | | по 2 на прибор |
| 16 | Кран шаровой угловой ½"×¾" для подключения стиральной и посудомоечной машины | аналог | | выбор заказчика | шт | 2 | | ОБ_02, ОБ_03 |
| | Трубопроводы | | | | | | | |
| 17 | Труба полипропиленовая PP-R PN20 Ø20×3,4 (В1) | ГОСТ 32415-2013 | | выбор заказчика | м | 27 | 0,17 | 20,1 + 4,3 + 10 % |
| 18 | Труба PP-R, армированная стекловолокном, PN20 Ø20×2,8 (Т3) | ГОСТ 32415-2013 | | выбор заказчика | м | 21,5 | 0,15 | 16,7 + 2,5 + 10 % |
| 19 | Труба канализационная ПП Ø40 (К1) | ГОСТ 32414-2013 | | выбор заказчика | м | 5 | | 2,6 + 1,6 + 10 % |
| 20 | Труба канализационная ПП Ø50 (К1) | ГОСТ 32414-2013 | | выбор заказчика | м | 15,5 | | 12,7 + 1,0 + 10 % |
| 21 | Труба канализационная ПП Ø110 (К1) | ГОСТ 32414-2013 | | выбор заказчика | м | 5 | | 3,9 + 0,4 + 10 % |
| | Фасонные части и выводы | | | | | | | |
| 22 | Отвод канализационный ПП 45° Ø40 | ГОСТ 32414-2013 | | выбор заказчика | шт | 4 | | 2 шт. на поворот |
| 23 | Отвод канализационный ПП 45° Ø50 | ГОСТ 32414-2013 | | выбор заказчика | шт | 12 | | 2 шт. на поворот |
| 24 | Отвод канализационный ПП 45° Ø110 | ГОСТ 32414-2013 | | выбор заказчика | шт | 10 | | 2 шт. на поворот |
| 25 | Тройник канализационный ПП 45° (врезки ветвей) | ГОСТ 32414-2013 | | выбор заказчика | шт | 7 | | |
| 26 | Ревизия канализационная ПП (после поворота трассы) | ГОСТ 32414-2013 | | выбор заказчика | шт | 7 | | доступ сохранить |
| 27 | Фитинги PP-R Ø20: тройники, угольники 90° (ветви и повороты В1, Т3) | ГОСТ 32415-2013 | | выбор заказчика | шт | 30 | | |
| 28 | Водорозетка PP-R Ø20×½" настенная, с креплением | ГОСТ 32415-2013 | | выбор заказчика | шт | 12 | | коды — лист выводов |
| | Узлы ввода, люки, короба | | | | | | | |
| 29 | Кран шаровой латунный Ду15 PN16 (отключение ввода) | аналог | | выбор заказчика | шт | 4 | | Ст В1-1, Ст Т3-1, Ст В1-2, Ст Т3-2 |
| 30 | Фильтр сетчатый косой Ду15 | аналог | | выбор заказчика | шт | 4 | | |
| 31 | Счётчик воды крыльчатый Ду15 (ХВ, ГВ), с поверкой | аналог | | выбор заказчика | шт | 4 | | пломба УК |
| 32 | Клапан обратный Ду15 | аналог | | выбор заказчика | шт | 4 | | |
| 33 | Люк ревизионный нажимной под плитку 300×400 мм | аналог | | выбор заказчика | шт | 4 | | к стоякам и арматуре |
| 34 | Звукоизоляция стояка К1 в коробе: рулонный звукоизоляционный материал ≥ 10 мм, обмотка стояка на высоту этажа | аналог | | выбор заказчика | м | 5,4 | | Ст К1-1, Ст К1-2 |
| 35 | Короб К1 над полом: профиль ПН/ПС, ГКЛВ 12,5 мм под плитку | аналог | | выбор заказчика | м | 6,8 | | сечение — лист разводки |

## Примечания

1. Форма 1 ГОСТ 21.110-2013, ширины граф изменены по п. 4.1. «Аналог» — аналог по характеристикам: модели внести до черновых работ, привязки выводов сверить по паспортам.
2. Бытовая техника не входит (показана арматура подключения), мойка — в комплекте кухни. Длины труб — трасса листа разводки + подъёмы + 10 %.
3. Стояк К1 в коробе — звукоизоляция стояка в коробе без жёсткого контакта короба с трубой.
4. Расчёт систем водоснабжения и канализации, диаметры магистралей и подбор оборудования выполняет проектная организация.

| | | | | | | | |
|---|---|---|---|---|---|---|---|
| | | | | | Проект: Четырёхкомнатная квартира | | |
| | Лист | № док. | Подпись | Дата | Спецификация сантехнического оборудования | Стадия | Лист | Листов |
| Дизайнер | Кырлан А.С. | | | 05.10.26 | | П | 20 | 111 |

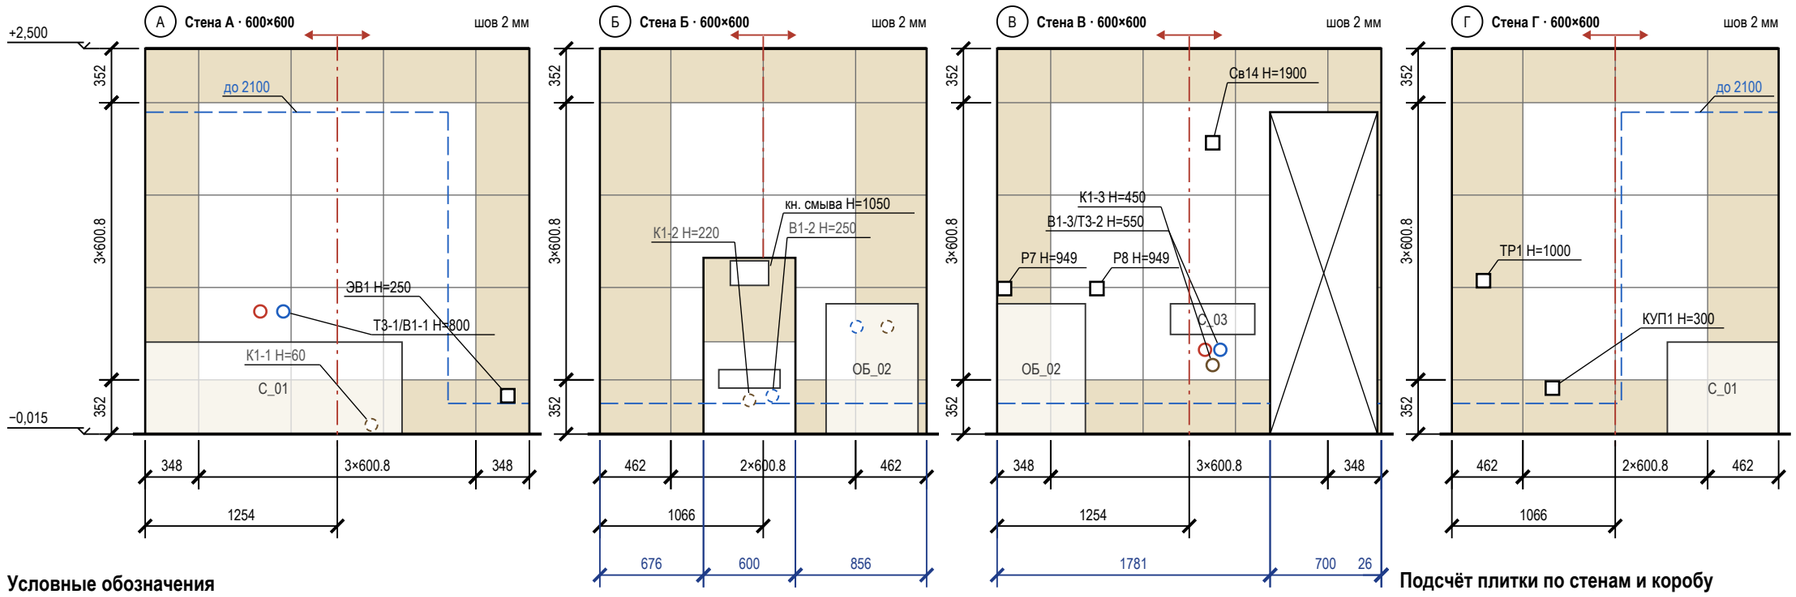


## Условные обозначения

- плитка целая; тонкая линия — шов
- плитка с подрезкой (размер — на цепочке)
- ось старта; стрелки — направление укладки
- верх гидроизоляции: 200 от ЧП, в мокрой зоне — «до …»
- проём — не облицовывается
- сантехприбор: габарит, высота по практике
- короб инсталляции, в нём кнопка смыва 250×160
- вывод В1 (код — в ведомости привязок)
- вывод ТЗ (код — в ведомости привязок)
- вывод К1 (код — в ведомости привязок)
- вывод за прибором / в коробе (не на сетке)
- электроточка: марка и Н — по листам ЭОМ
- отметка уровня, м: ±0,000 — чистый пол жилых помещений
- низ потолка; серая полоса — стена без плитки
- (А) обозначение стены А–Г (как на развёртках)

## Примечания

1. Вид изнутри, стены по часовой стрелке А → Г. Высоты — от чистого пола (−0,015), отметки — от ±0,000. Раскладка от чистовых размеров (штукатурка 10 + клей 5 + плитка 9 мм), подрезки чистые; старт — от оси стены, ряды от середины (две подрезки).
2. Облицовка до потолка (+2,500).
3. Точки из таблицы сдвигов переносятся до черновой разводки: смеситель — по оси пары В1 + ТЗ; вывод на оси прибора — вместе с прибором, иначе старт раскладки — на ось прибора.
4. За приборами и в коробе (К1-1, В1-2, К1-2, В1-4, К1-4) — штриховым кольцом.
5. Гидроизоляция: 200 мм от ЧП по периметру; над ванной — до 2100 и 300 мм за борт (СП 29.13330.2011, п. 7.2 — на высоту замачивания); углы — лентой; акт скрытых работ, пролив.
6. Короб 600×1150×230: лицо 600 мм от оси кнопки смыва, боковины, полка; углы — запил 45° или профиль; за коробом плитку не кладут.
7. Наружные углы: ст. Б: 2 — запил 45°; ст. В: 2 — профиль.
8. Люки: Л1 (ст. Б, 600×600, нажимной) — кромки дверцы по швам сетки.

## Подсчёт плитки по стенам и коробу

| Поверхность | L × H, мм | S, м² | Целых | Подр. | С запасом | Подрезки: край / верх, мм |
|---|---|---|---|---|---|---|
| стена А | 2507 × 2515 | 6,43 | 9 | 16 | 28 | 348 / 348; 352 |
| стена Б | 2132 × 2515 | 4,79 | 2 | 18 | 22 | 462 / 462; 352 |
| короб (ст. Б) | 600×1150×230 | 1,36 | 1 | 6 | 8 | лицо 600; бок. 230 |
| стена В | 2507 × 2515 | 4,96 | 6 | 19 | 28 | 348 / 348; 352 |
| стена Г | 2132 × 2515 | 5,48 | 6 | 14 | 22 | 462 / 462; 352 |
| **Итого** | | **23,01** | **24** | **73** | **108** | |

## Сдвиг точек под раскладку

| Точка (ВК, ЭОМ) | Стена | Проект: от угла / Н | Под раскладку: от угла / Н | Сдвиг, мм |
|---|---|---|---|---|
| ТЗ-1/В1-1 | А | 826 / 800 | 952 / 655 | +126 на шов; Н −145 |
| ЭВ1 | А | 2366 / 250 | 2459 / 353 | +93 в центр плитки; Н +103 |
| В1-3/ТЗ-2 | В | 1406 / 550 | 1555 / 655 | +149 на шов; Н +105 |
| К1-3 | В | 1406 / 450 | 1253 / 353 | −153 в центр плитки; Н −97 |
| Св14 | В | 1406 / 1900 | 1555 / 1860 | +149 на шов; Н −40 |
| ТР1 | Г | 206 / 1000 | 162 / 956 | −44 в центр плитки; Н −44 |
| КУП1 | Г | 656 / 300 | 765 / 353 | +109 в центр плитки; Н +53 |


| | | | | |
|---|---|---|---|---|
| | Лист | № док. | Подпись | Дата |
| Дизайнер | Кырлан А.С. | | | 05.10.26 |

Проект: Четырёхкомнатная квартира

Раскладка плитки. Ванная комната. Развёртки стен

| Стадия | Лист | Листов |
|---|---|---|
| П | 21 | 111 |

выпуск 05.10.2026 № 05166c8858 · стр. 21 из 111

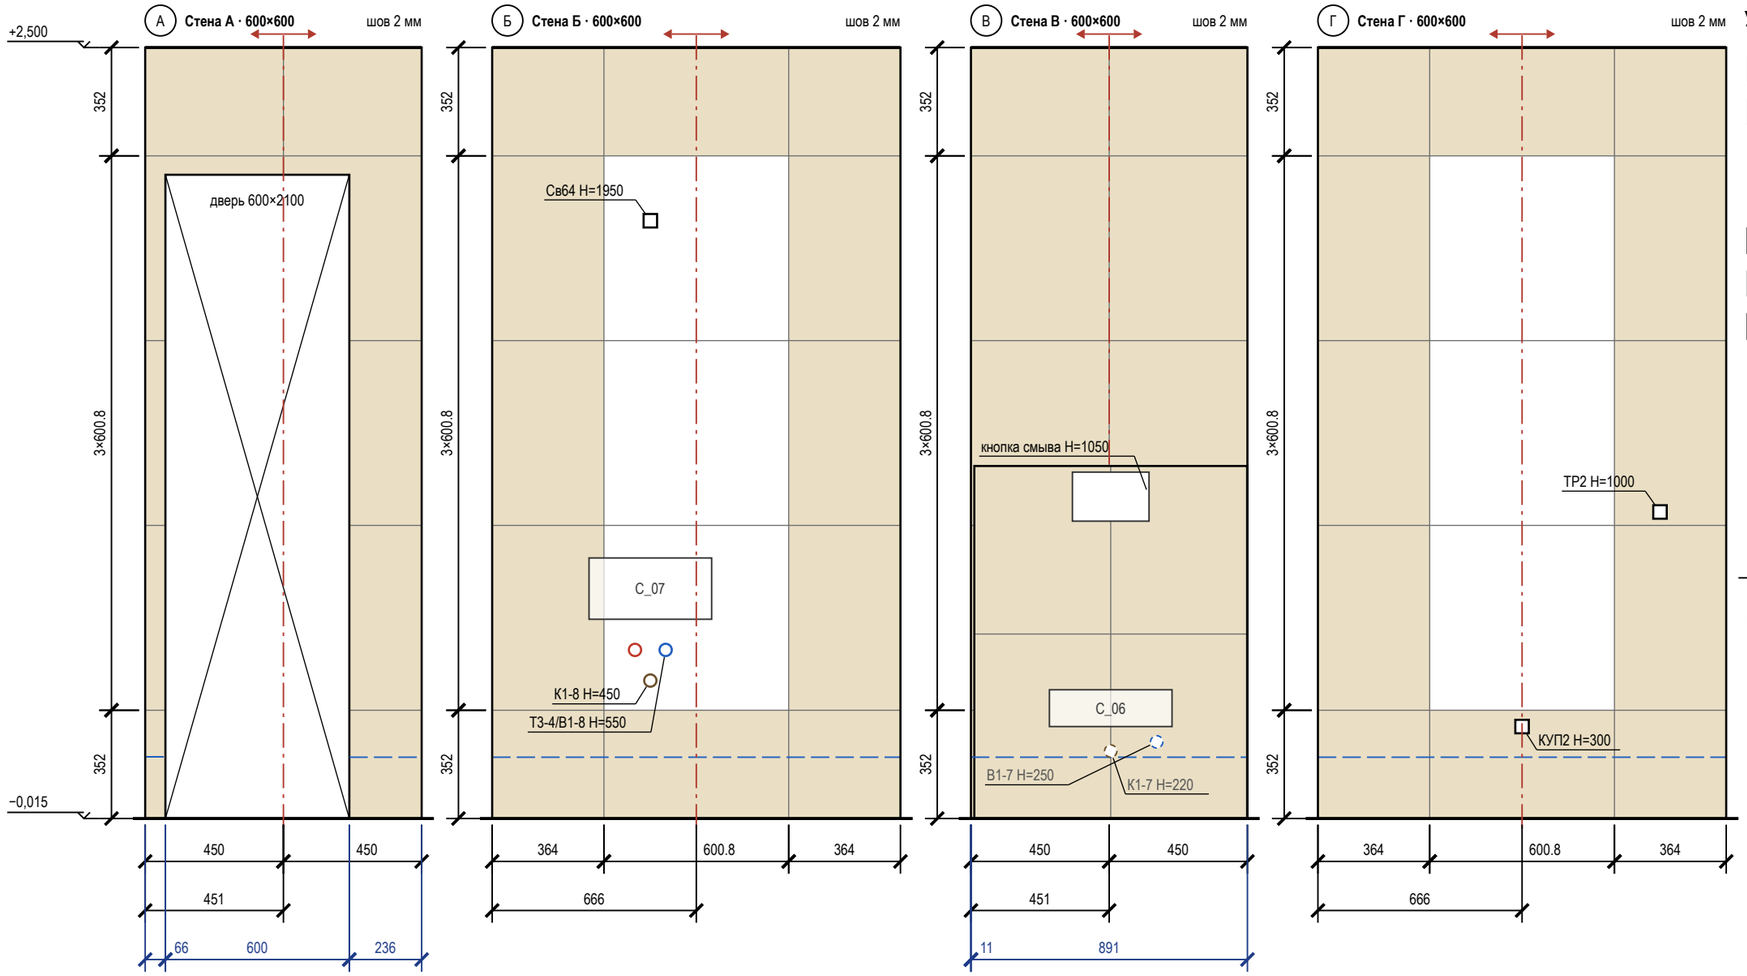


## Условные обозначения

- плитка целая; тонкая линия — шов
- плитка с подрезкой (размер — на цепочке)
- ось старта; стрелки — направление укладки
- верх гидроизоляции: 200 от ЧП, в мокрой зоне — «до …»
- проём — не облицовывается
- сантехприбор: габарит, высота по практике
- короб инсталляции, в нём кнопка смыва 250×160
- вывод В1 (код — в ведомости привязок)
- вывод Т3 (код — в ведомости привязок)
- вывод К1 (код — в ведомости привязок)
- вывод за прибором / в коробе (не на сетке)
- электроточка: марка и Н — по листам ЭОМ
- отметка уровня, м: ±0,000 — чистый пол жилых помещений
- низ потолка; серая полоса — стена без плитки
- (А) обозначение стены А–Г (как на развёртках)

## Подсчёт плитки по стенам и коробу

| Поверхность | L × H, мм | S, м² | Целых | Подр. | С запасом | Подрезки: край / верх, мм |
|---|---|---|---|---|---|---|
| стена А | 902 × 2515 | 1,13 | 0 | 10 | 11 | 450 / 450; 352 |
| стена Б | 1332 × 2515 | 3,47 | 3 | 12 | 17 | 364 / 364; 352 |
| стена В | 902 × 2515 | 1,37 | 0 | 10 | 11 | 450 / 450; 352 |
| короб (ст. В) | 890×1150×230 | 1,76 | 0 | 10 | 11 | лицо 444 / 444; бок. 230 |
| стена Г | 1332 × 2515 | 3,47 | 3 | 12 | 17 | 364 / 364; 352 |
| **Итого** | | **11,19** | **6** | **54** | **67** | |

## Сдвиг точек под раскладку

| Точка (ВК, ЭОМ) | Стена | Проект: от угла / Н | Под раскладку: от угла / Н | Сдвиг, мм |
|---|---|---|---|---|
| Т3-4/В1-8 | Б | 516 / 550 | 666 / 655 | +150 в центр плитки; Н +105 |
| К1-8 | Б | 516 / 450 | 666 / 353 | +150 в центр плитки; Н −97 |
| Св64 | Б | 516 / 1950 | 666 / 1860 | +150 в центр плитки; Н −90 |
| КУП2 | Г | 666 / 300 | 666 / 353 | Н +53 |
| ТР2 | Г | 1116 / 1000 | 1269 / 956 | +153 в центр плитки; Н −44 |

## Примечания


1. Вид изнутри, стены по часовой стрелке А → Г. Высоты — от чистого пола (−0,015), отметки — от ±0,000. Раскладка от чистовых размеров (штукатурка 10 + клей 5 + плитка 9 мм), подрезки чистые; старт — от оси стены, ряды от середины (две подрезки).
2. Облицовка до потолка (+2,500).
3. Точки из таблицы сдвигов переносятся до черновой разводки: смеситель — по оси пары В1 + Т3; вывод на оси прибора — вместе с прибором, иначе старт раскладки на ось прибора.
4. За приборами и в коробе (В1-7, К1-7) — штриховым кольцом.
5. Гидроизоляция: 200 мм от ЧП по периметру; углы — лентой; акт скрытых работ, пролив.
6. Короб 890×1150×230: лицо 444 / 444 мм от оси кнопки смыва, боковины, полка; углы — запил 45° или профиль; за коробом плитку не кладут.
7. Между коробом и углом полоса 11 мм — довести короб до угла.
8. Наружные углы: ст. А: 2 — профиль.

| | | | | | |
|---|---|---|---|---|---|
| | | | | | Проект: Четырёхкомнатная квартира |
| | Лист | № док. | Подпись | Дата | Раскладка плитки. Санузел. Развёртки стен |
| Дизайнер | Кырлан А.С. | | | 05.10.26 | |

| Стадия | Лист | Листов |
|---|---|---|
| П | 22 | 111 |

## Примечания

1. Размеры проёмов и привязки — в миллиметрах от чистых граней стен до отделки; привязка — от угла того помещения, со стороны которого стоит размер. Размер в ведомости — ширина × высота проёма от чистого пола 0,000.
2. Марки в кружках — типы заполнения проёмов (ГОСТ 21.501-2018, п. 5.3.2); одна марка — один типоразмер; количество сверено с планом.
3. Открывание: Л — петли слева, П — справа, если смотреть со стороны, куда открывается полотно (на себя).
4. Дверные блоки обычного монтажа (Д-1…Д-5) заказывать после чистовой стяжки и штукатурки, проёмы перемерить; монтажный зазор коробки 10–15 мм на сторону, откос от угла помещения до коробки — не менее 50 мм.
5. Размеры проёмов и привязки сняты со скана плана заказчика и на объекте не замерены (обмерный план — лист 3).
6. Экспликация помещений — лист 3; в марках помещений — номер и площадь, м².
7. Привязка проёма к углу помещения меньше 1 мм на листе, размер на плане не показан: Д-2 — 50 мм; Д-1 — 100 мм; Д-3 — 90 мм.

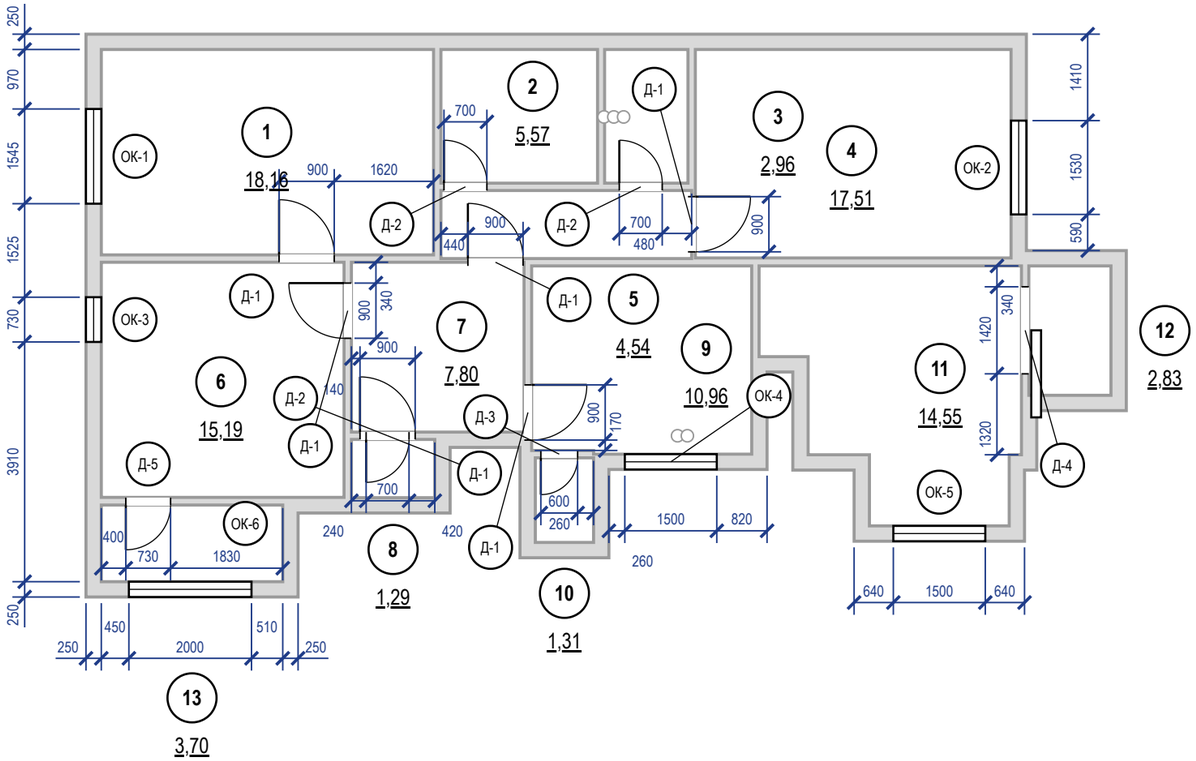



## Ведомость заполнения проёмов

| Марка | Наименование, обозначение | Проём ш×в, мм | Кол. | Откр. | Отделка полотна | Фурнитура | Прим. |
|---|---|---|---|---|---|---|---|
| Д-1 | Блок дверной внутренний, ГОСТ 475-2016 | 900×2100 | 6 | П, П, П, Л, П, П | | петли, ручка с защёлкой | б/п |
| Д-2 | Блок дверной внутренний, ГОСТ 475-2016 | 700×2100 | 3 | П, П, Л | | петли, ручка с защёлкой, фиксатор WC | пом. 2; порог 15 |
| Д-3 | Блок дверной внутренний, ГОСТ 475-2016 | 600×2100 | 1 | Л | | петли, ручка с защёлкой, фиксатор WC | порог 15 |
| Д-4 | Дверь раздвижная, ГОСТ 475-2016 | 1420×2100 | 1 | | | раздвижная система, ручки-купе | пом. 12; б/п |
| Д-5 | Блок дверной внутренний, ГОСТ 475-2016 | 730×2100 | 1 | Л | | петли, ручка с защёлкой | порог 30 |
| ОК-1 | Блок оконный, ГОСТ 23166-2021 | 1545×1600 | 1 | | | | низ 800 |
| ОК-2 | Блок оконный, ГОСТ 23166-2021 | 1530×1600 | 1 | | | | низ 800 |
| ОК-3 | Блок оконный, ГОСТ 23166-2021 | 730×1600 | 1 | | | | низ 800 |
| ОК-4 | Блок оконный, ГОСТ 23166-2021 | 1500×1600 | 1 | | | | пом. 9; низ 800 |
| ОК-5 | Блок оконный, ГОСТ 23166-2021 | 1500×1600 | 1 | | | | пом. 11; низ 900 |
| ОК-6 | Блок оконный, ГОСТ 23166-2021 | 2000×1700 | 1 | | | | низ 900 |

| | | | | | |
|---|---|---|---|---|---|
| | | | | | Проект: Четырёхкомнатная квартира |
| | Лист | № док. | Подпись | Дата | План размещения дверей |
| Дизайнер | Кырлан А.С. | | | 05.10.26 | |

| Стадия | Лист | Листов |
|---|---|---|
| П | 23 | 111 |

выпуск 05.10.2026 № 05166c8858 · стр. 23 из 111

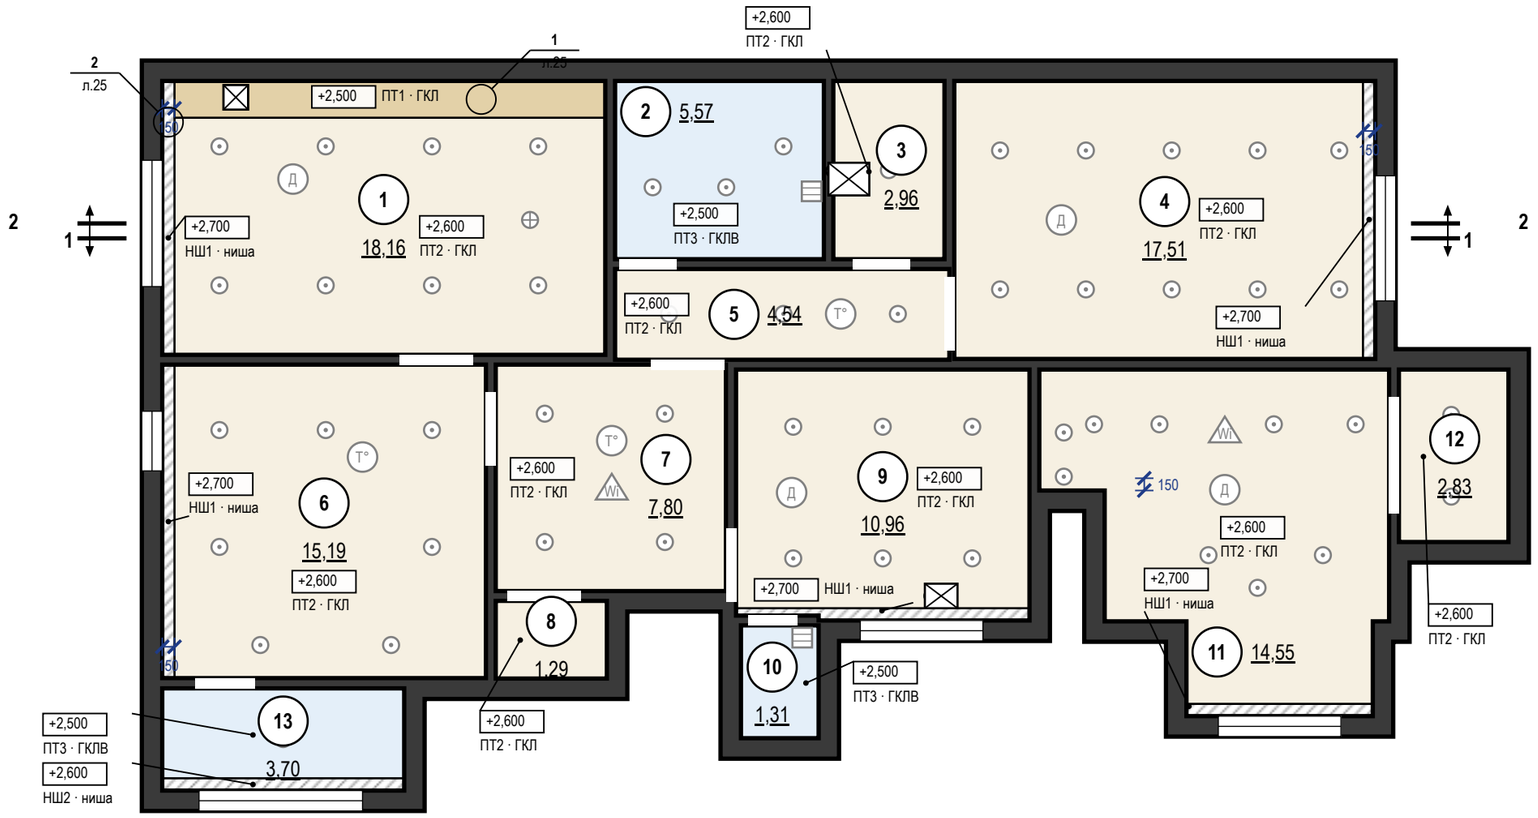


## Ведомость потолков

| Пом. | Марка | Конструкция | Низ | S, м² | Q |
|---|---|---|---|---|---|
| 1 | ПТ1 | ГКЛ П113, короб LED | +2,500 | 2,37 | Q3 |
| 1 | ПТ2 | ГКЛ П113 | +2,600 | 15,29 | Q3 |
| 1 | НШ1 | ниша под шторы 150×100 | +2,700 | 0,50 | |
| 2 | ПТ3 | ГКЛВ П113 | +2,500 | 5,57 | Q3 |
| 3 | ПТ2 | ГКЛ П113 | +2,600 | 2,96 | Q3 |
| 4 | ПТ2 | ГКЛ П113 | +2,600 | 17,00 | Q3 |
| 4 | НШ1 | ниша под шторы 150×100 | +2,700 | 0,51 | |
| 5 | ПТ2 | ГКЛ П113 | +2,600 | 4,54 | Q3 |
| 6 | ПТ2 | ГКЛ П113 | +2,600 | 14,61 | Q3 |
| 6 | НШ1 | ниша под шторы 150×100 | +2,700 | 0,58 | |
| 7 | ПТ2 | ГКЛ П113 | +2,600 | 7,80 | Q3 |
| 8 | ПТ2 | ГКЛ П113 | +2,600 | 1,29 | Q3 |
| 9 | ПТ2 | ГКЛ П113 | +2,600 | 10,48 | Q3 |
| 9 | НШ1 | ниша под шторы 150×100 | +2,700 | 0,48 | |
| 10 | ПТ3 | ГКЛВ П113 | +2,500 | 1,31 | Q3 |
| 11 | ПТ2 | ГКЛ П113 | +2,600 | 14,21 | Q3 |
| 11 | НШ1 | ниша под шторы 150×100 | +2,700 | 0,34 | |
| 12 | ПТ2 | ГКЛ П113 | +2,600 | 2,83 | Q3 |
| 13 | ПТ3 | ГКЛВ П113 | +2,500 | 3,26 | Q3 |
| 13 | НШ2 | ниша под шторы 150×100 | +2,600 | 0,44 | |
| | | **Итого** | | **106,37** | |

## Ведомость вырезов и закладных в потолке

| Марка | Устройство | Кол. | Пом. |
|---|---|---|---|
| | Светильник встраиваемый (марки — план освещения) | 56 | 1, 2, 3, 4, 5, 6, 7, 8, 9, 10, 11, 12, 13 |
| | Светильник подвесной (марки — план освещения) | 1 | 1 |
| ИП1, ИП2, ИП6, ИП7 | Извещатель дымовой | 4 | 1, 4, 9, 11 |
| ИП3…ИП5 | Извещатель тепловой | 3 | 5, 6, 7 |
| АР1, АР2 | Точка доступа Wi-Fi, PoE | 2 | 7, 11 |
| ВР1, ВР3 | Решётка вытяжная (вентилятор) | 2 | 2, 10 |
| | Люк ревизии 500×400, 400×300, 300×300 | 4 | 1, 3, 9, 11 |

## Примечания

1. За отметку ±0,000 принят уровень чистого пола сухих помещений (готовое покрытие), а не существующего пола; пол пом. 2, 10, 13 — −0,015, −0,030; верх плиты перекрытия −0,170 — расчётный по пирогу пола, не замерен; существующий пол снимается до плиты, его отметка не замерена. Отметки в прямоугольниках — низ потолка; низ плиты перекрытия +2,700, +2,600. Марка потолка — одна конструкция и отметка на весь альбом.
2. Потолки ГКЛ — каркасная система П113: подвесы через 1000, несущие профили через 500, основные через 1200 мм; листы — поперёк несущих профилей. В помещениях 2, 10, 13 — ГКЛВ на оцинкованном каркасе.
3. LED-лента в алюминиевом профиле посередине карниза короба шириной 450 мм (узел 1, лист 25); длина по плану: пом. 1 — 5,4 м (в плане освещения 5); пом. 11 — 5,4 м.
4. Ниши под шторы 150×100 мм — на всю длину стены с окном; карниз — на закладной до обшивки (узел 2, лист 25).
5. Примыкание к стенам: теневой шов 15 мм, техзазор 3 мм — пом. 1, 11, по стенам, выровненным штукатуркой (узел 1); пом. 2, 3, 4, 5, 6, 7, 8, 9, 10, 12, 13 — разделительная лента.
6. Светильники и потолочные устройства — подложка с планов освещения, слаботочных систем и вентиляции (положение — по ним); вырезы и закладные — по ведомости на листе, до обшивки; отверстия не совмещать с профилями, глубина корпуса светильника до 70 мм.
7. Разрезы 1–1, 2–2 и узлы — на листе 25; высоты мебели и дверных блоков сверены с низом потолка в разрезах.
8. Шпаклевание ГКЛ и условия приёмки — Q3: рассеянный дневной свет, осмотр с 2 м; боковой свет не оценивается.
9. Люки ревизии 500×400, 400×300, 300×300 мм — по центру блоков питания LED (ревизия, ревизия, блок питания LED БП1, блок питания LED БП1; координаты — план освещения).


| | | | | | |
|---|---|---|---|---|---|
| | | | | | Проект: Четырёхкомнатная квартира |
| | Лист | № док. | Подпись | Дата | План потолков |
| Дизайнер | Кырлан А.С. | | | 05.10.26 | |

| Стадия | Лист | Листов |
|---|---|---|
| П | 24 | 111 |

выпуск 05.10.2026 № 05166c8858 · стр. 24 из 111


## Разрез 1–1 (М 1:40)

Пом. 1 Зал; линия разреза — план потолков, лист 24

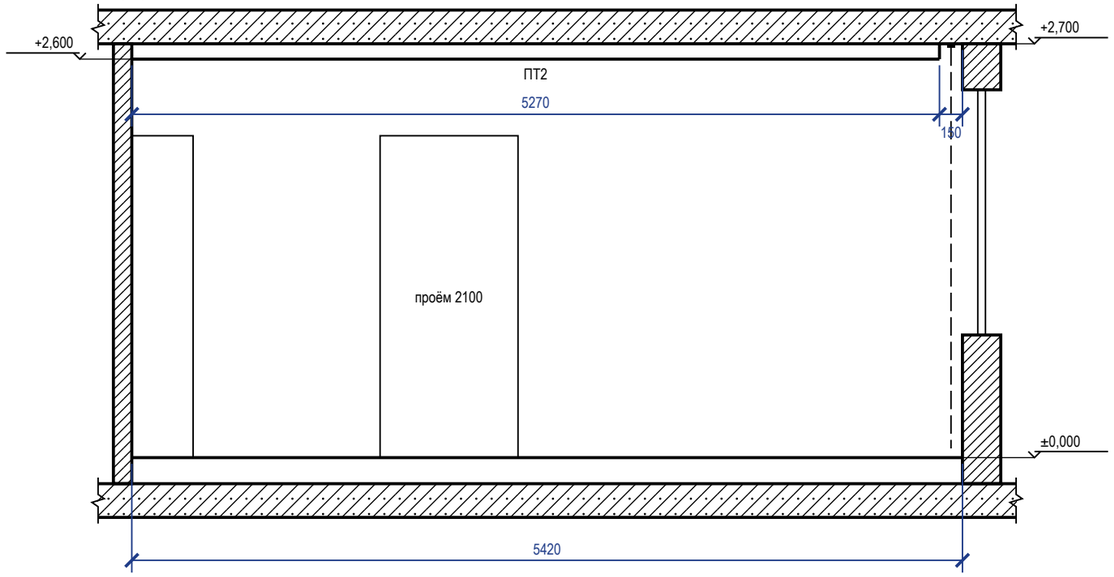



## Разрез 2–2 (М 1:40)

Пом. 4 Детская 1; линия разреза — план потолков, лист 24

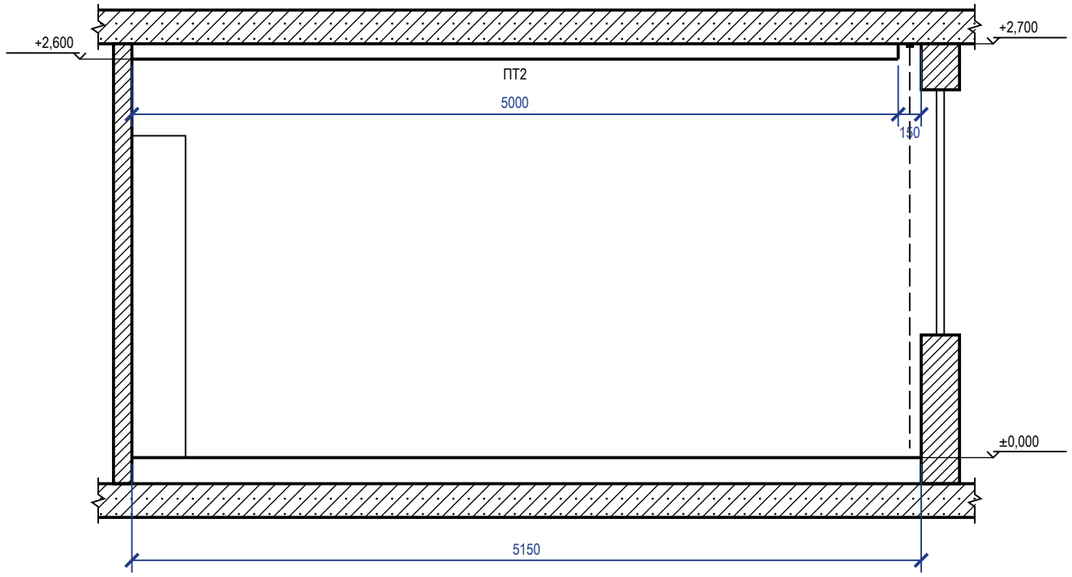


## 1 Короб с LED-подсветкой, теневой шов (М 1:10)


Пом. 1, 11; карниз 150×100, щель под свет 60 мм

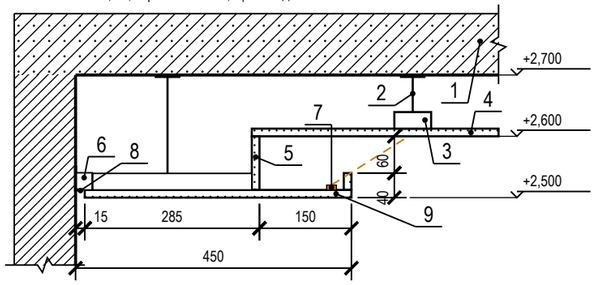


1 — плита перекрытия
2 — подвес прямой, шаг 1000 мм
3 — ПП 60×27: несущие через 500, основные через 1200 мм
4 — ГКЛ 12,5 по П113 — верхний уровень
5 — задняя стенка и бортик карниза — ГКЛ 12,5
6 — ПН 28×27 по периметру, к стене через 500 мм
7 — LED-лента в алюминиевом профиле
8 — теневой профиль: шов 15 мм, зазор 3 мм
9 — низ короба — ГКЛ 12,5 по ПП 60×27

## 2 Ниша под шторы (М 1:10)

Пом. 1, 4, 6, 9, 11, 13; без подсветки; закладные под карниз — до обшивки

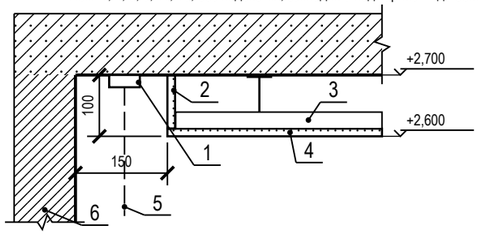


1 — карниз (шина), высота с верхом портьеры 80 мм
2 — стенка ниши — ГКЛ 12,5
3 — ПП 60×27 — каркас короба
4 — низ короба нижнего уровня — ГКЛ 12,5
5 — портьера
6 — стена с окном

## Условные обозначения

- плита перекрытия в сечении
- стена в сечении
- потолок ГКЛ в сечении; под линией — марка потолка (план потолков)
- мебель и дверные проёмы за секущей плоскостью; число — марка и верх от чистого пола, мм
- портьера в нише под шторы


## Примечания

1. Разрезы — по линиям 1–1, 2–2 на плане потолков (лист 24). Отметки — от ±0,000 чистого пола, м; размеры — мм.
2. Высоты мебели и дверных блоков за секущей плоскостью сверены с низом потолка над ними: верх ниже низа короба и поля.
3. ГКЛ 12,5 мм по каркасу П113; перепад уровней и бортик карниза — ГКЛ по ПП 60×27 (узел 1). Ниша под шторы — на всю длину стены с окном, карниз на закладной до обшивки (узел 2).
4. Толщины плит перекрытия и пирога пола показаны условно.

| | | | | | |
|---|---|---|---|---|---|
| | | | | | Проект: Четырёхкомнатная квартира |
| | Лист | № док. | Подпись | Дата | |
| Дизайнер | Кырлан А.С. | | | 05.10.26 | Разрезы и узлы потолков |

| Стадия | Лист | Листов |
|---|---|---|
| П | 25 | 111 |

выпуск 05.10.2026 № 05166c8858 · стр. 25 из 111

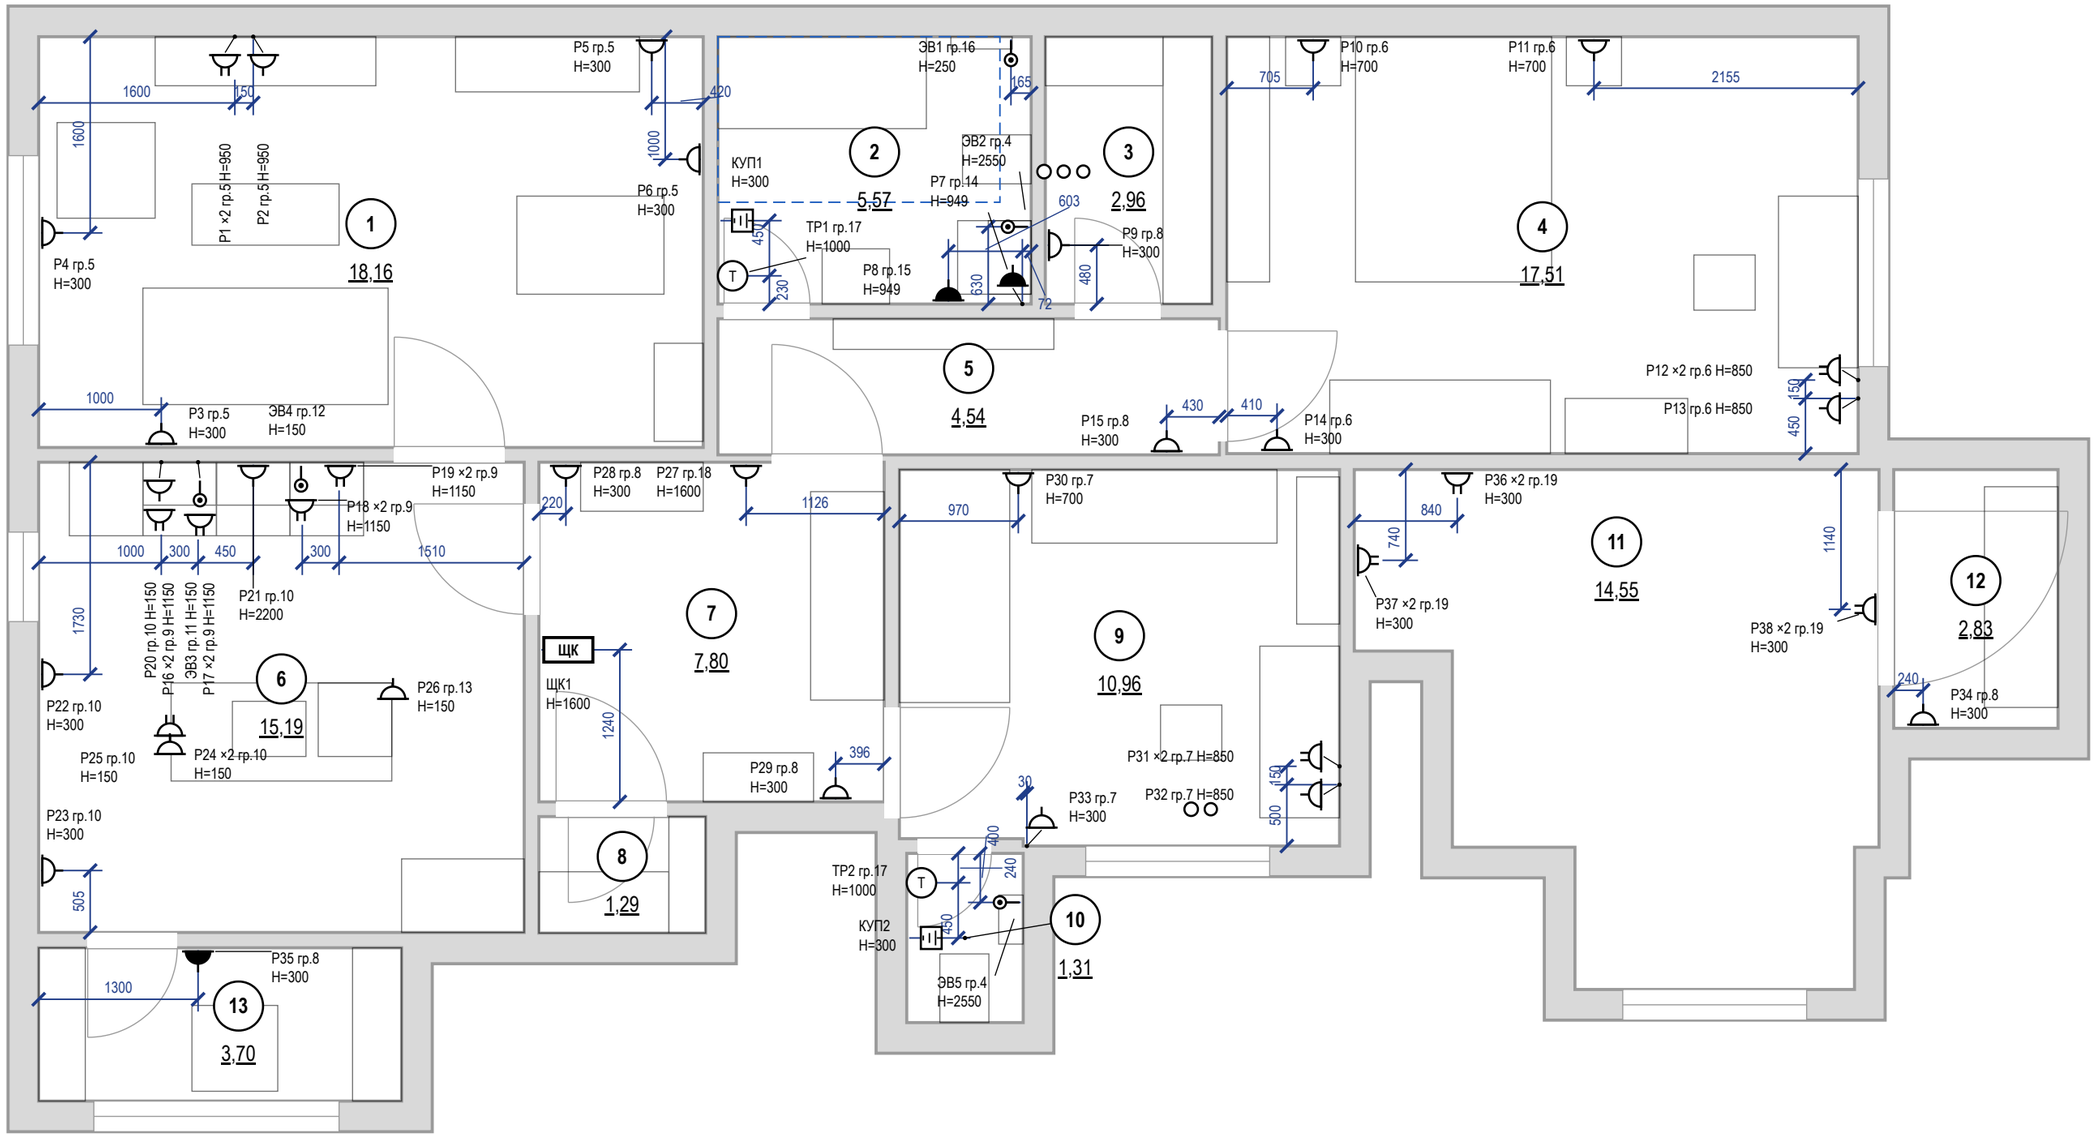



## Примечания

1. За отметку 0,000 принят уровень чистого пола. Высоты Н — от чистого пола до оси изделия; привязки — от чистовой грани стены до оси механизма (у рамки на несколько постов — до оси рамки).
2. Высота установки, не указанная на плане: розетки — 300 мм от чистого пола; выводы кабеля — по паспорту прибора.
3. Розетки в санузле — только вне зон 0–2 (ПУЭ 7.1.48, ГОСТ Р 50571.7.701-2024), IP44, через УЗО 30 мА.
4. Розеточные и мокрые линии — через УЗО или дифавтомат с током утечки не более 30 мА (ПУЭ 7.1.79); в санузле выполнить ДСУП (ПУЭ 7.1.87–7.1.88).
5. Кабель — медный, исполнение нг(А)-LS (ГОСТ 31565-2012); скрытая прокладка только горизонтально и вертикально, фактические трассы зафиксировать исполнительной схемой до закрытия отделкой.
6. Расчёт нагрузок, токов КЗ, селективности и сечений — по проекту ЭОМ организации с допуском СРО; лист задаёт состав, расположение и группы.
7. Ведомости электроточек, изделий, светильников и расшифровка клавиш — лист «Ведомость электроточек и изделий».

| | | | | | |
|---|---|---|---|---|---|
| | | | | | Проект: Четырёхкомнатная квартира |
| | Лист | № док. | Подпись | Дата | План розеток и электровыводов |
| Дизайнер | Кырлан А.С. | | | 05.10.26 | |

| Стадия | Лист | Листов |
|---|---|---|
| П | 26 | 111 |

выпуск 05.10.2026 № 05166c8858 · стр. 26 из 111

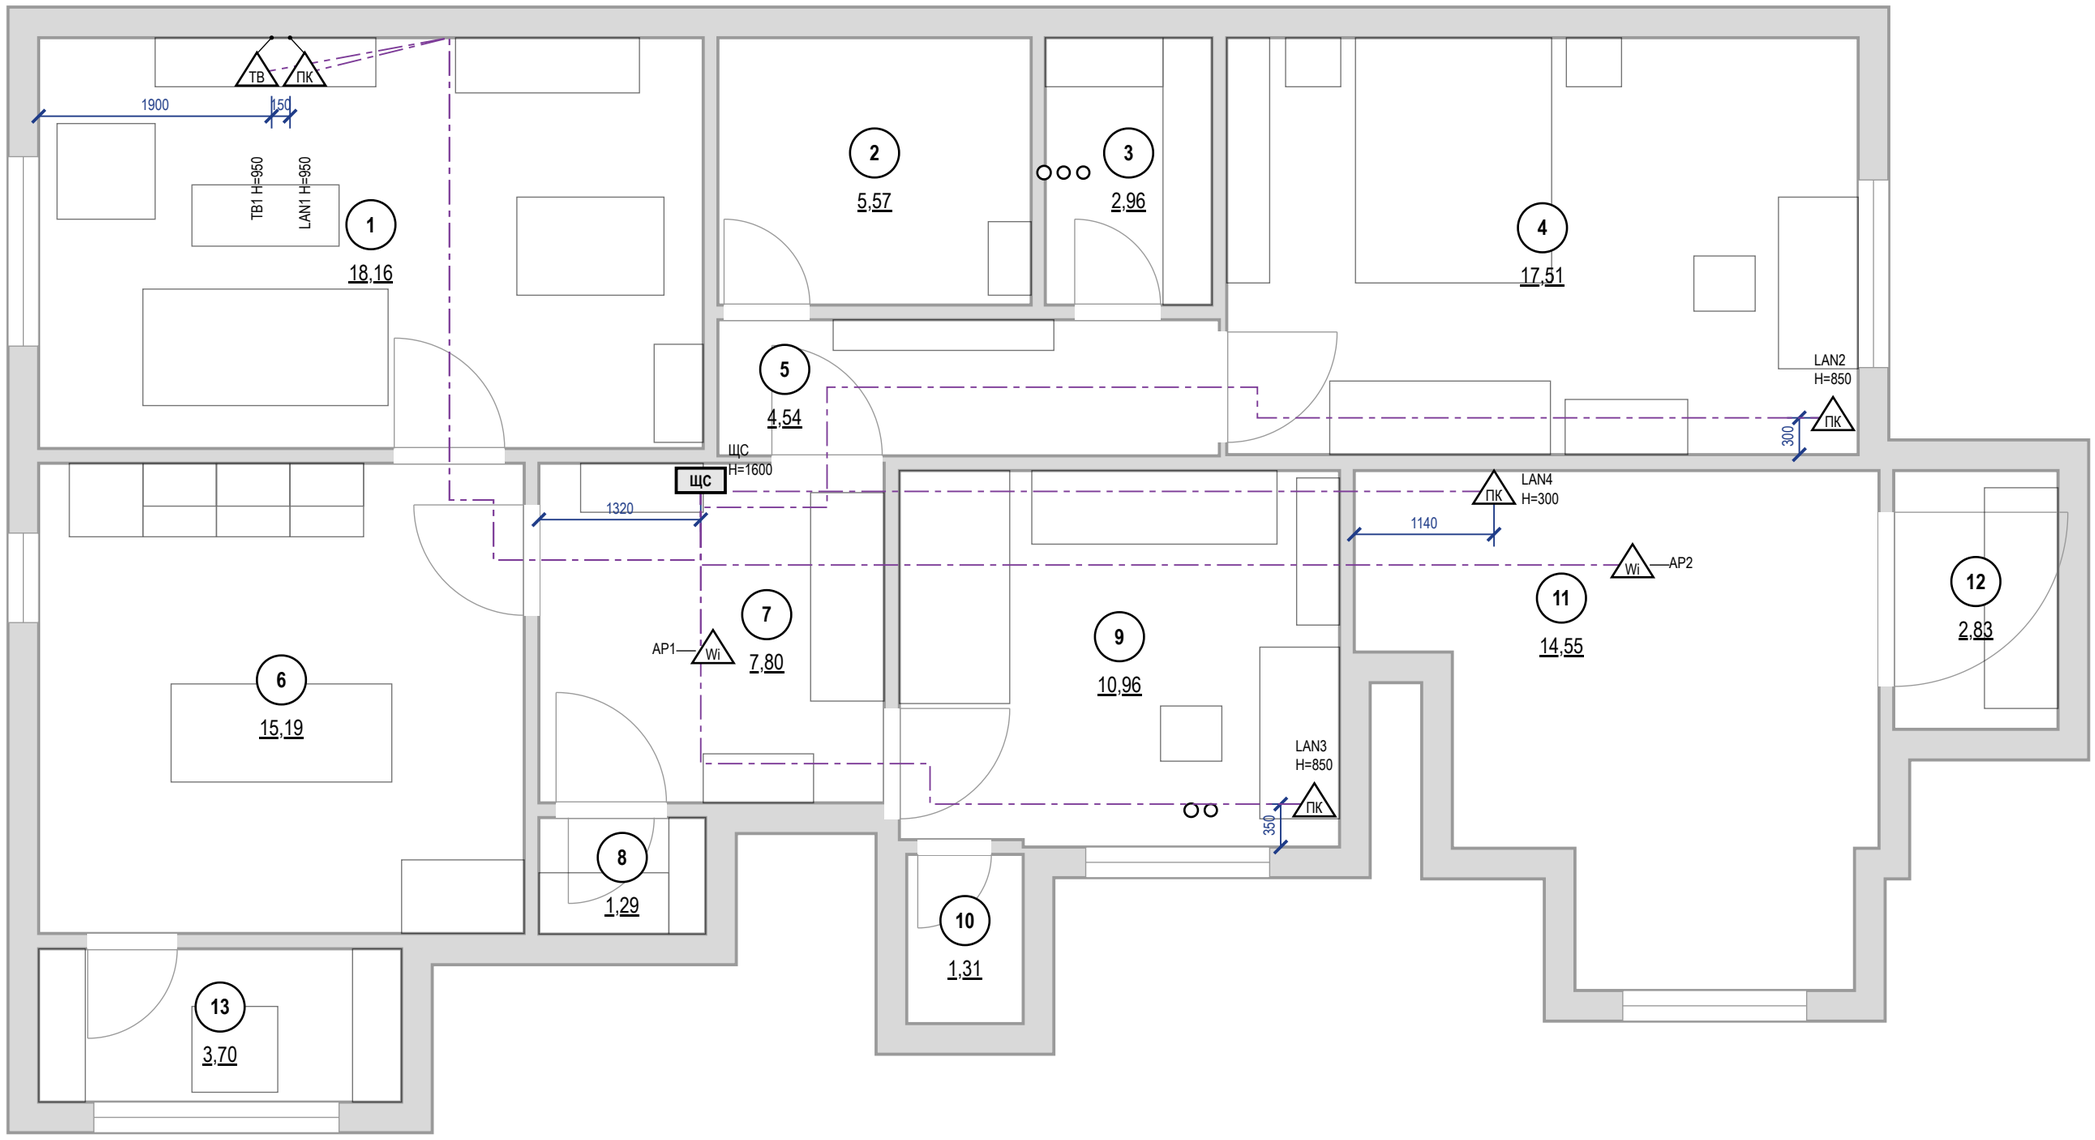



## Примечания

1. За отметку 0,000 принят уровень чистого пола. Высоты Н — от чистого пола до оси изделия; привязки — от чистовой грани стены до оси механизма (у рамки на несколько постов — до оси рамки).
2. Высота установки, не указанная на плане: розетки LAN и ТВ — 300 мм от чистого пола.
3. Слаботочные кабели — отдельно от силовых: в своей трубе или лотке, при параллельной прокладке не ближе 100 мм к силовым, пересечения под прямым углом; каждую точку — отдельным кабелем от ЩС без скруток.
4. Трассы на листе — принципиальные; фактические зафиксировать исполнительной схемой до закрытия отделкой. Силовые линии, УЗО 30 мА, ДСУП, кабель нг(А)-LS — по листам розеток и щита.
5. Проект силовой части и расчёт токов КЗ — по проекту ЭОМ; слаботочная часть согласуется с провайдером и управляющей компанией (домофон, коллективное ТВ).

| | | | | | |
|---|---|---|---|---|---|
| | | | | | Проект: Четырёхкомнатная квартира |
| | Лист | № док. | Подпись | Дата | |
| Дизайнер | Кырлан А.С. | | | 05.10.26 | План слаботочных сетей |

| Стадия | Лист | Листов |
|---|---|---|
| П | 27 | 111 |

выпуск 05.10.2026 № 0516c8858 · стр. 27 из 111

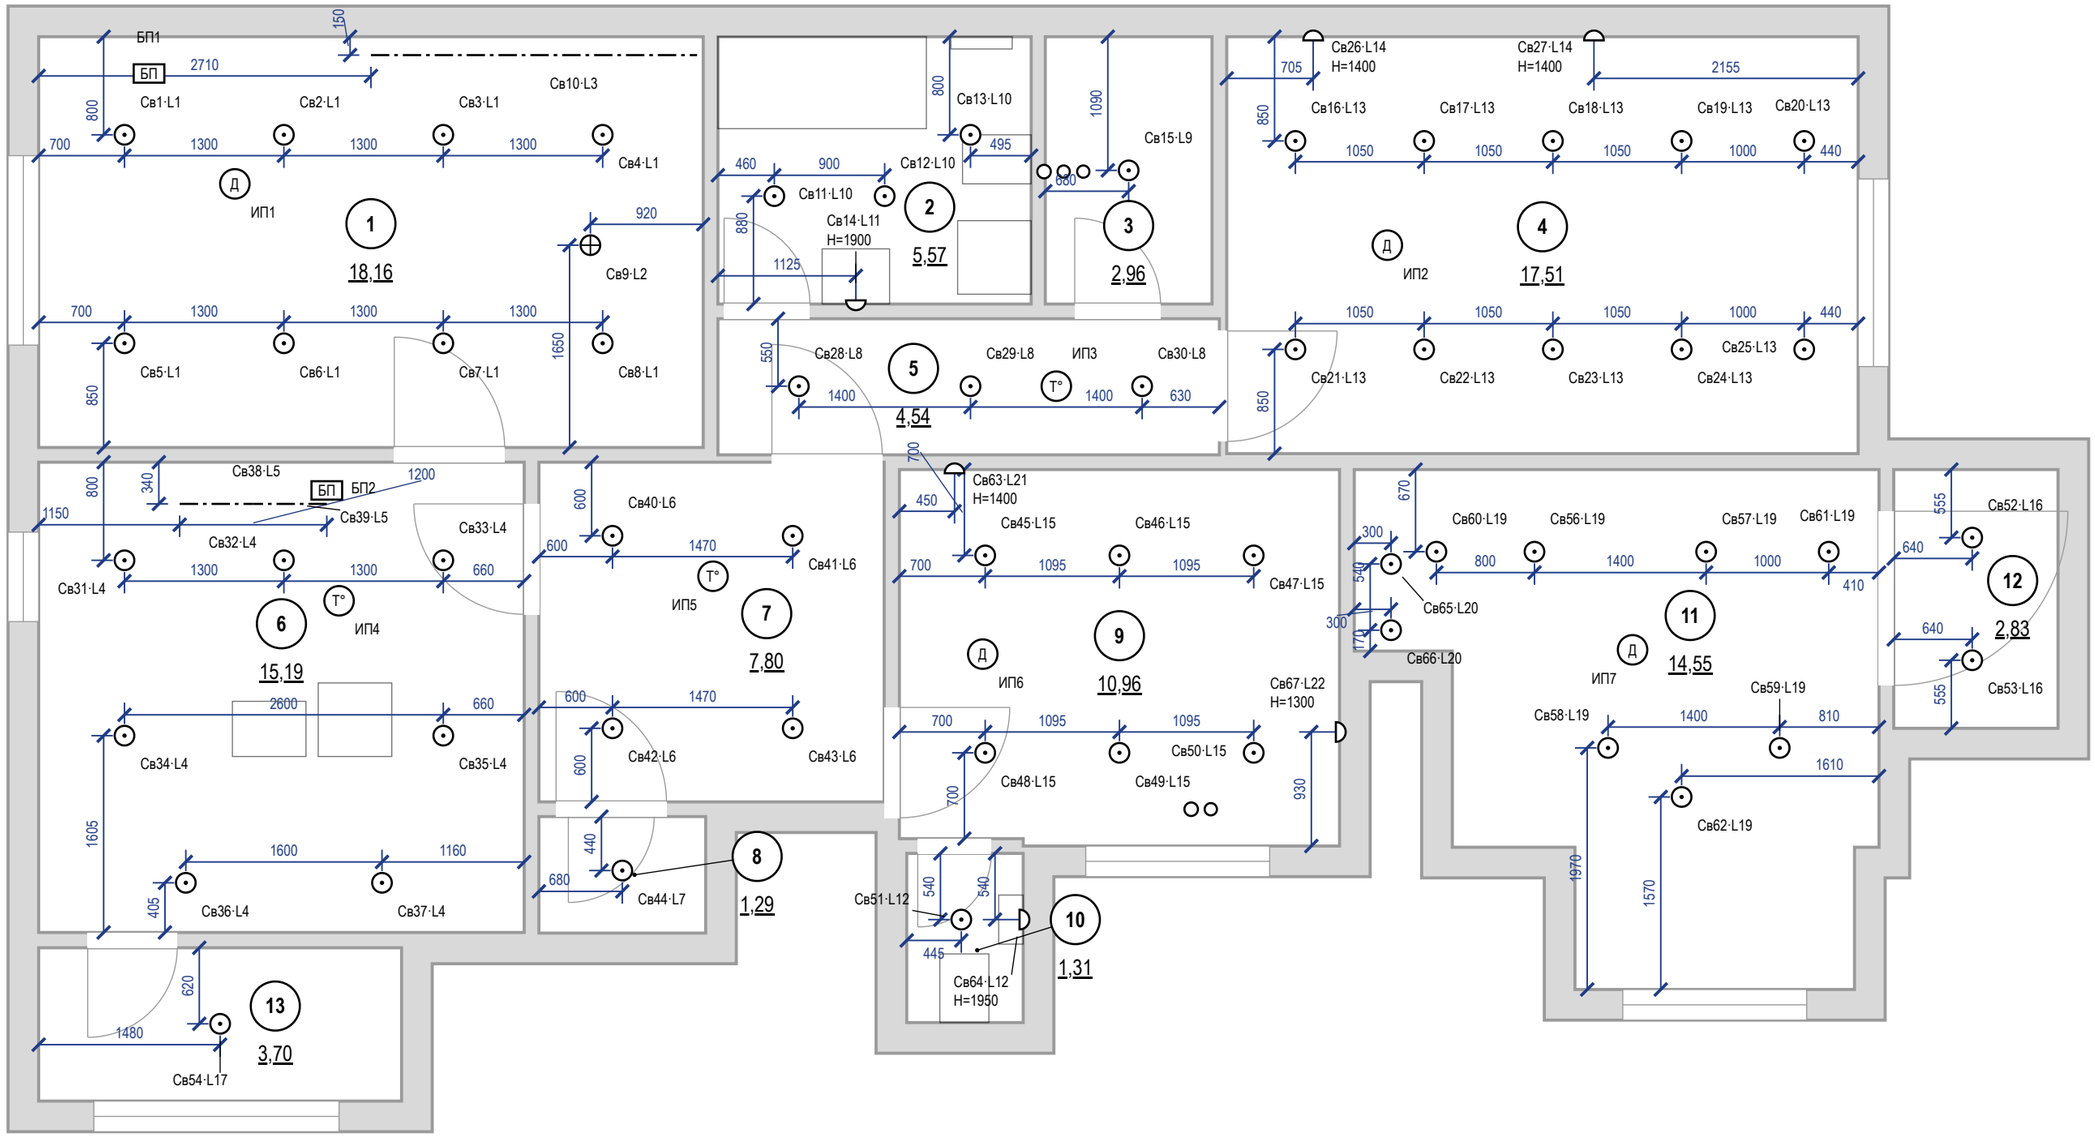


## Примечания

1. За отметку 0,000 принят уровень чистого пола. Высоты Н — от чистого пола до оси изделия; привязки — от чистовой грани стены до оси механизма (у рамки на несколько постов — до оси рамки).
2. Высота установки, не указанная на плане: светильники — на потолке; настенные — по отметке Н у знака. Привязки — до оси светильника от чистовой грани стены, по рядам.
3. Освещённость: Ен — СанПиН 1.2.3685-21, табл. 5.52 (на полу); Ф треб. = Ен·S/(U·MF) при U = 0,5 и MF = 0,71 (СП 52.13330.2016, табл. 4.3) — оценка, не светотехнический расчёт. Декоративная подсветка в Ф не входит.
4. Во влажных помещениях — светильники не ниже IP44; в зонах 0–2 ванной — по ГОСТ Р 50571.7.701-2024 (зона 1 — IPX5).
5. Розеточные и мокрые линии — через УЗО или дифавтомат с током утечки не более 30 мА (ПУЭ 7.1.79); в санузле выполнить ДСУП (ПУЭ 7.1.87–7.1.88).
6. Кабель — медный, исполнение нг(A)-LS (ГОСТ 31565-2012); скрытая прокладка только горизонтально и вертикально, фактические трассы зафиксировать исполнительной схемой до закрытия отделкой.
7. Расчёт нагрузок, токов КЗ, селективности и сечений — по проекту ЭОМ организации с допуском СРО; лист задаёт состав, расположение и группы.
8. Ведомость светильников — лист «Ведомость электроточек и изделий».

| | | | | | |
|---|---|---|---|---|---|
| | | | | | Проект: Четырёхкомнатная квартира |
| | Лист | № док. | Подпись | Дата | |
| Дизайнер | Кырлан А.С. | | | 05.10.26 | План освещения |
| | | | | | Стадия: П; Лист: 28; Листов: 111 |

выпуск 05.10.2026 № 05166c8858 · стр. 28 из 111

## Спецификация светильников

| Поз. | Марки | Наименование | Установка | Кол. | P, Вт | Σ P, Вт | Ф, лм | Тц, К | Ra | Угол, ° | IP | Дим. | Группа | Пом. |
|---|---|---|---|---|---|---|---|---|---|---|---|---|---|---|
| 1 | Св1–Св8, Св16–Св19, Св20, Св21–Св24, Св25, Св31–Св37, Св56–Св62 | Встраиваемый точечный | в ГКЛ, корпус ≤ 70 мм | 32 | 12 | 384 | 1000 | 3000 | 90 | — | 20 | — | L1, L4, L13, L19 | 1, 4, 6, 11 |
| 2 | Св9 | Подвесной | подвес, низ H=1600 | 1 | 15 | 15 | 1200 | 2700 | 90 | — | 20 | — | L2 | 1 |
| 3 | Св10 | Лента светодиодная 24 В | в коробе, профиль с рассеивателем | 5 м | 9,6/м | 48 | 900/м | 2700 | 90 | — | 20 | да | L3 | 1 |
| 4 | Св11, Св12, Св13, Св51 | Встраиваемый точечный | в ГКЛ, корпус ≤ 70 мм | 4 | 6 | 24 | 500 | 3000 | 90 | — | 44 | — | L10, L12 | 2, 10 |
| 5 | Св14, Св64 | Светильник над зеркалом, драйвер встроен | над зеркалом, H=1900, 1950 | 2 | 8 | 16 | 600 | 3000 | 90 | — | 44 | — | L11, L12 | 2, 10 |
| 6 | Св15, Св40–Св44, Св52, Св53, Св65, Св66 | Встраиваемый точечный | в ГКЛ, корпус ≤ 70 мм | 10 | 6 | 60 | 500 | 3000 | 90 | — | 20 | — | L6, L7, L9, L16, L20 | 3, 7, 8, 11, 12 |
| 7 | Св26, Св27, Св63 | Настенный (бра) | на стене, H=1400 | 3 | 6 | 18 | 400 | 2700 | 90 | 60 | 20 | — | L14, L21 | 4, 9 |
| 8 | Св28–Св30 | Встраиваемый точечный | в ГКЛ, корпус ≤ 70 мм | 3 | 5 | 15 | 400 | 3000 | 90 | — | 20 | — | L8 | 5 |
| 9 | Св38, Св39 | Линейный светильник | на поверхности | 1,2 м | 8 | 16 | 700 | 3000 | 90 | — | 20 | — | L5 | 6 |
| 10 | Св45–Св50 | Встраиваемый точечный | в ГКЛ, корпус ≤ 70 мм | 6 | 13 | 78 | 1100 | 3000 | 90 | — | 20 | — | L15 | 9 |
| 11 | Св67 | Бра подсветки рабочего места, стол M_35 | на стене, H=1300 | 1 | 7 | 7 | 450 | 3000 | 90 | 60 | 20 | — | L22 | 9 |
| 12 | Св54 | Встраиваемый точечный | в ГКЛ, корпус ≤ 70 мм | 1 | 9 | 9 | 800 | 3000 | 90 | — | 44 | — | L17 | 13 |
| | | **Итого** | | **63 шт + 6,2 м** | | **690** | | | | | | | | |

## LED-ленты, линейные светильники и блоки питания

| Марка | Пом. | L, м | U, В | Вт/м | Σ P, Вт | БП | P БП, Вт | Загр., % | Питание | Доступ к БП |
|---|---|---|---|---|---|---|---|---|---|---|
| Св10 | 1 | 5 | 24 | 9,6 | 48 | БП1 | 100 | 48 | с одного конца | люк 300×300 в коробе потолка у стены A |
| Св38 | 6 | 0,6 | 24 | — | 8 | БП2 | 30 | 53 | встроенный ввод | в навесном модуле M_25, съёмная панель |
| Св39 | 6 | 0,6 | 24 | — | 8 | БП2 | 30 | 53 | встроенный ввод | в навесном модуле M_25, съёмная панель |

## Сценарии освещения

| Пом. | Сценарий | Группы и уровни, % | Чем включается |
|---|---|---|---|
| 1 | Вечер | L1 общий свет (споты) — 0; L2 подвес над обеденным столом — 100; L3 лента в карнизе (диммер) — 50 | S1, S2 светорегулятор |
| 1 | Гости | L1 общий свет (споты) — 100; L2 подвес над обеденным столом — 100; L3 лента в карнизе (диммер) — 100 | S1, S2 светорегулятор |
| 1 | Кино | L1 общий свет (споты) — 0; L2 подвес над обеденным столом — 0; L3 лента в карнизе (диммер) — 20 | S2 светорегулятор |
| 1 | Уборка | L1 общий свет (споты) — 100; L2 подвес над обеденным столом — 100; L3 лента в карнизе (диммер) — 0 | S1 |

## Слои света

общий — равномерный свет помещения, по норме освещённости

рабочий — местный свет задачи: столешница, зеркало, чтение у кровати

акцентный — подсветка потолка, стен и ниш; не входит в поток общего света


## Слои света по помещениям

| Пом. | Помещение | Слои света и группы включения (марки светильников) | Тц, К | Ra | Σ P, Вт | Сцен. |
|---|---|---|---|---|---|---|
| 1 | Зал | общий — L1 (Св1–Св8); рабочий — L2 (Св9); акцентный — L3 (Св10) | 2700 / 3000 | 90 | 159 | 4 |
| 2 | Ванная комната | общий — L10 (Св11, Св12, Св13); рабочий — L11 (Св14) | 3000 | 90 | 26 | — |
| 3 | Тёмная комната | общий — L9 (Св15) | 3000 | 90 | 6 | — |
| 4 | Детская 1 | общий — L13 (Св16–Св19, Св20, Св21–Св24, Св25); рабочий — L14 (Св26, Св27) | 2700 / 3000 | 90 | 132 | — |
| 5 | Коридор | общий — L8 (Св28–Св30) | 3000 | 90 | 15 | — |
| 6 | Кухня | общий — L4 (Св31–Св37); рабочий — L5 (Св38, Св39) | 3000 | 90 | 100 | — |
| 7 | Прихожая-коридор | общий — L6 (Св40–Св43) | 3000 | 90 | 24 | — |
| 8 | Гардеробная 2 | общий — L7 (Св44) | 3000 | 90 | 6 | — |
| 9 | Детская 2 | общий — L15 (Св45–Св50); рабочий — L21 (Св63), L22 (Св67) | 2700 / 3000 | 90 | 91 | — |
| 10 | Санузел | общий — L12 (Св51); рабочий — L12 (Св64) | 3000 | 90 | 14 | — |
| 11 | Гостиная | общий — L19 (Св56–Св62); акцентный — L20 (Св65, Св66) | 3000 | 90 | 96 | — |
| 12 | Гардеробная 1 | общий — L16 (Св52, Св53) | 3000 | 90 | 12 | — |
| 13 | Балкон 1 | общий — L17 (Св54) | 3000 | 90 | 9 | — |

## Примечания

1. Позиции и марки Св — те же, что на плане освещения (лист 28) и в ведомости светильников (лист «Ведомость электроточек и изделий»); группы L — по плану выключателей (лист 30).
2. Модели светильников не назначены: подбор по графам спецификации — поток, Тц, Ra, угол, IP и диммирование не хуже указанных, мощность не больше; встраиваемые — под глубину короба (графа «Установка»). IP 20 — сухие помещения.
3. Длина LED-ленты в карнизе — по линии карниза плана потолков (лист 24); Σ P = Вт/м × длина. Блок питания загружен не больше чем на 80 %; лента 24 В длиннее 10 м питается с двух концов; доступ к блоку питания — люк ревизии 300×300 мм или место, указанное в таблице.
4. Сценарии: уровень — доля максимальной яркости группы, %; 0 — группа выключена. Уровень ниже 100 % — только у групп на светорегуляторе (задний фронт, TE) с диммируемыми драйверами и блоками питания.
5. Мощность и поток — по паспортам принятых изделий, Σ P — установленная мощность освещения. Оценка освещённости — на плане освещения; это не светотехнический расчёт.


| | | | | | |
|---|---|---|---|---|---|
| | | | | | Проект: Четырёхкомнатная квартира |
| | Лист | № док. | Подпись | Дата | |
| Дизайнер | Кырлан А.С. | | | 05.10.26 | Спецификация светильников и сценарии освещения |
| | | | | | Стадия: П; Лист: 29; Листов: 111 |

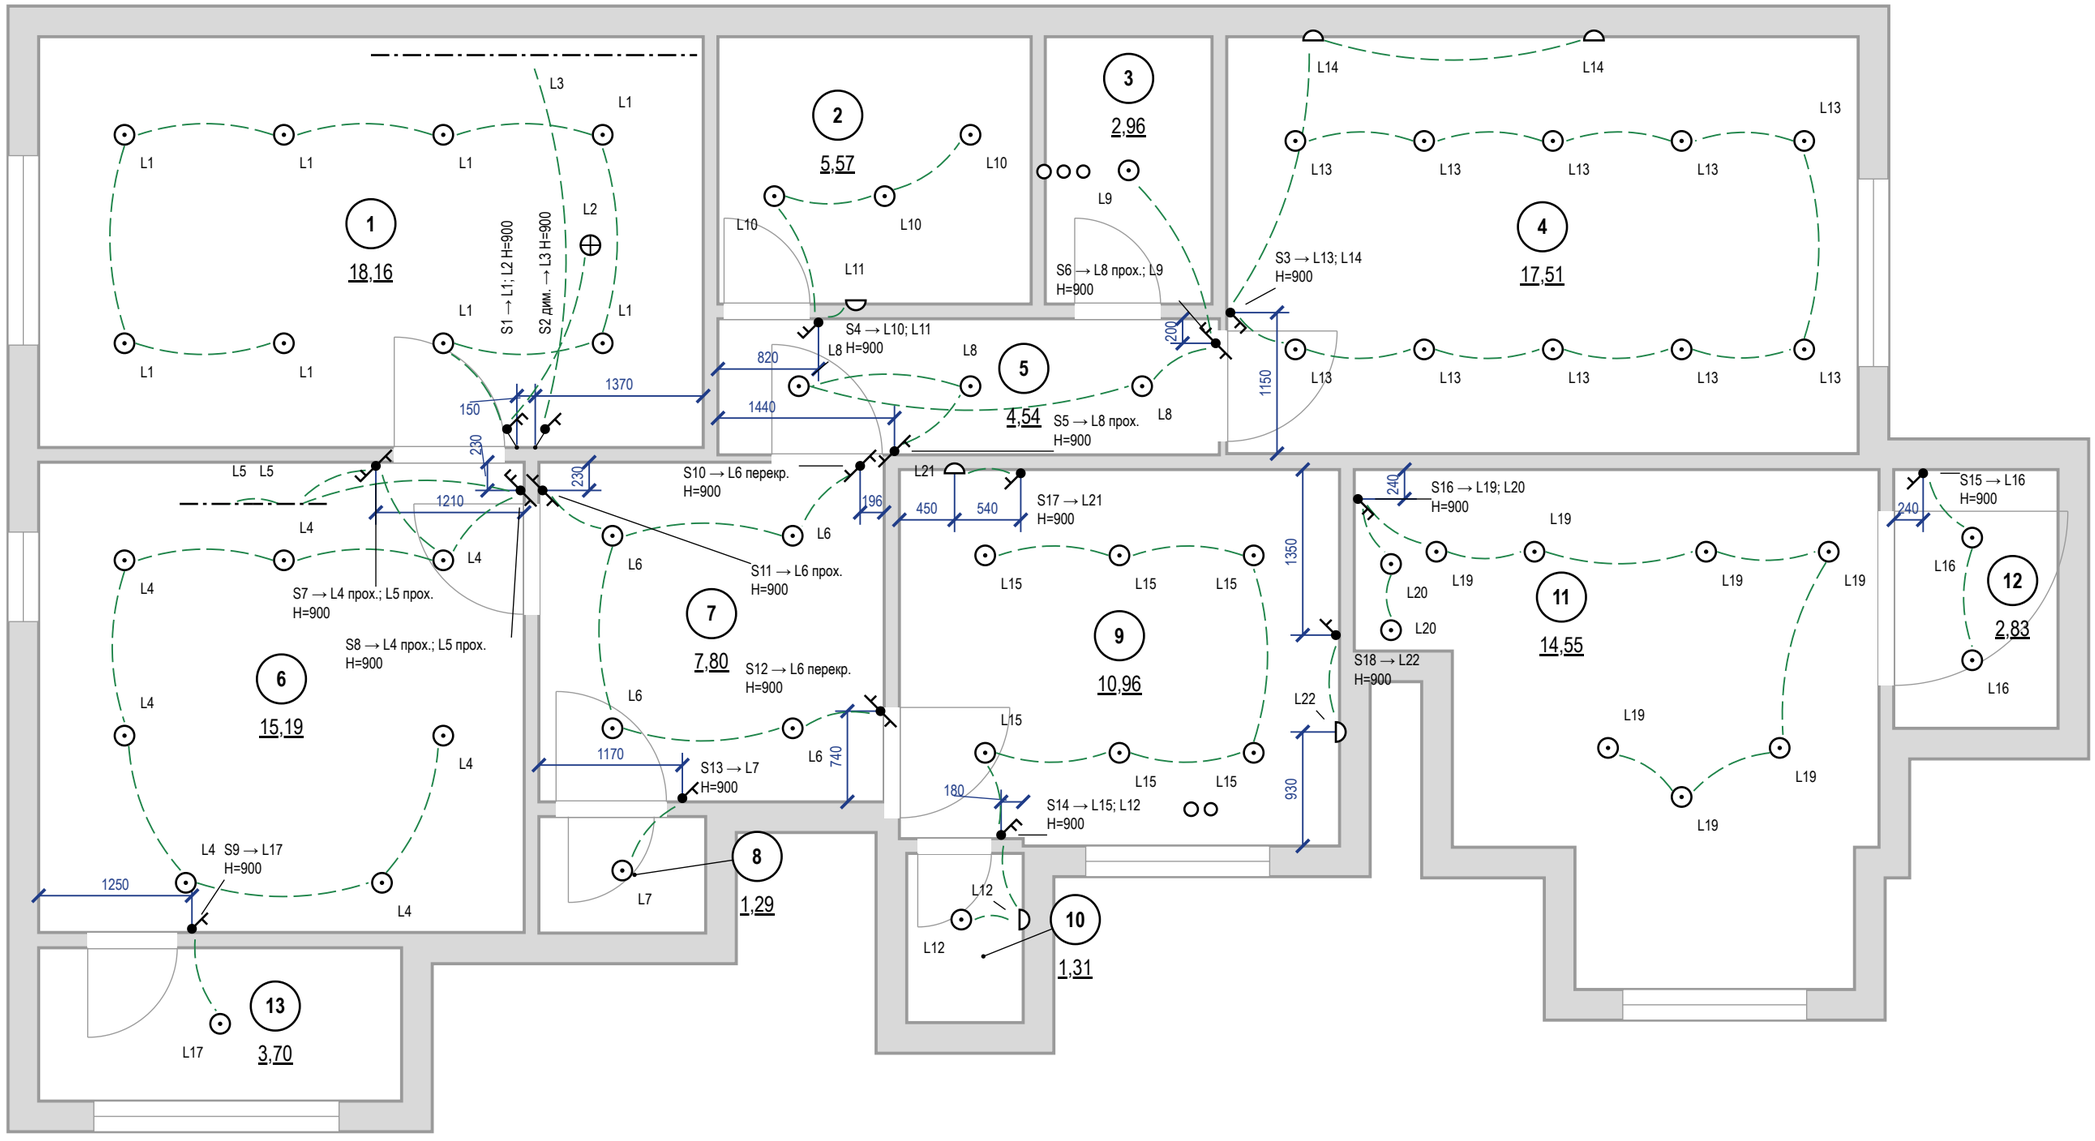


## Примечания

1. За отметку 0,000 принят уровень чистого пола. Высоты H — от чистого пола до оси изделия; привязки — от чистовой грани стены до оси механизма (у рамки на несколько постов — до оси рамки).
2. Высота установки, не указанная на плане: выключатели — 900 мм от чистого пола, со стороны дверной ручки (ПУЭ 7.1.51).
3. Линии связи показывают, какой выключатель какую группу L включает; это не трасса кабеля. Трасса — принципиальная, фактическую зафиксировать исполнительной схемой.
4. Группы из нескольких мест (L8 — S5, S6; L4 — S7, S8; L5 — S7, S8; L6 — S10, S11, S12): на крайних местах — проходные клавиши, на промежуточных перекрёстные; механизмы — в ведомости изделий.
5. Светорегулятор — по заднему фронту (для LED-драйверов), совместимость с драйверами проверить до закупки.
6. Розеточные и мокрые линии — через УЗО или дифавтомат с током утечки не более 30 мА (ПУЭ 7.1.79); в санузле выполнить ДСУП (ПУЭ 7.1.87–7.1.88).
7. Кабель — медный, исполнение нг(A)-LS (ГОСТ 31565-2012); скрытая прокладка только горизонтально и вертикально, фактические трассы зафиксировать исполнительной схемой до закрытия отделкой.
8. Расчёт нагрузок, токов КЗ, селективности и сечений — по проекту ЭОМ организации с допуском СРО; лист задаёт состав, расположение и группы.
9. Расшифровка клавиш и ведомость изделий — лист «Ведомость электроточек и изделий».

| | | | | | |
|---|---|---|---|---|---|
| | | | | | Проект: Четырёхкомнатная квартира |
| | Лист | № док. | Подпись | Дата | Управление светильниками |
| Дизайнер | Кырлан А.С. | | | 05.10.26 | Стадия: П; Лист: 30; Листов: 111 |

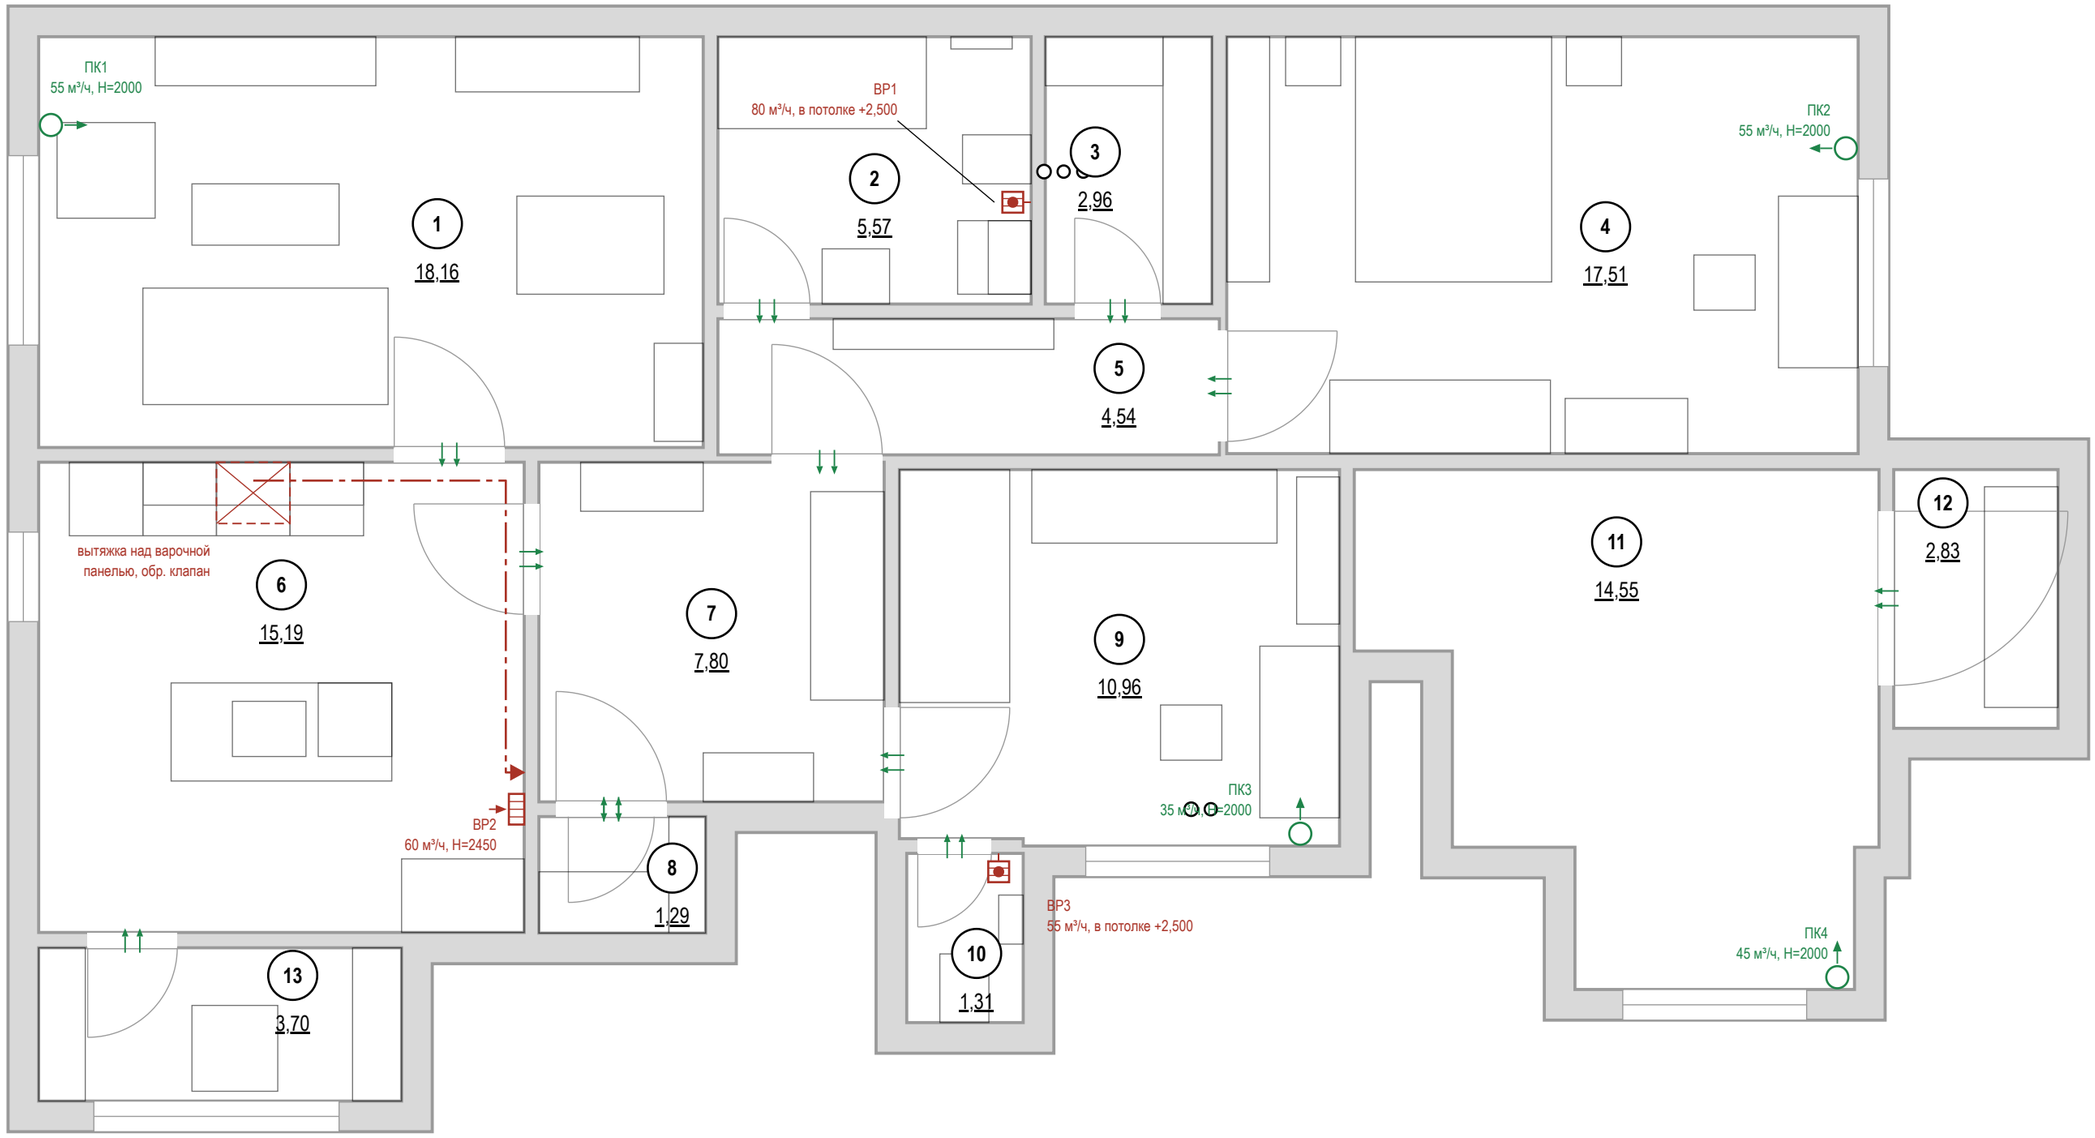



## Примечания

1. Расчёт систем ОВ и подбор оборудования — проектная организация с допуском СРО; лист даёт места, трассы и привязки.
2. Нормы вытяжки — СП 54.13330.2022 (Изм. 1, 2), табл. 7.1: кухня с электроплитой 60 м³/ч, с газовой 100; ванная и совмещённый санузел 50; уборная 25; гардеробная 0,2 ч⁻¹. Приток в жилые — 3 м³/ч на 1 м² (менее 20 м² общей площади на человека), иначе 30 м³/ч на человека.
3. Вентканалы и шахты не сужать, не переносить и не закрывать; вентилятор и кухонная вытяжка — через обратный клапан, без перекрытия естественной тяги.
4. Проектные расходы — не ниже нормы, вытяжка сведена с притоком вентиляторами мокрых помещений. Клапаны — в простенке у окна, центр 2000 мм, не над кроватью, не ближе 300 мм к стоякам отопления; типоразмер — на расход.
5. Под подшивным потолком вытяжка — в потолке, воздуховодом за потолком до канала. Кухонная вытяжка в воздухообмен не включена: воздуховод не менее Ø125 в коробе, вход в канал отдельный.
6. Переток — зазор под полотнами межкомнатных дверей или переточная решётка.
7. Кондиционирование заданием не предусмотрено; при установке трассы фреона и дренажа (не менее 40 мм/м, в К1 через сифон) и питание заложить до черновых работ.
8. Привязки оборудования — по паспортам приобретённых моделей, до черновых работ.

| | | | | | |
|---|---|---|---|---|---|
| | | | | | Проект: Четырёхкомнатная квартира |
| | Лист | № док. | Подпись | Дата | План вентиляции |
| Дизайнер | Кырлан А.С. | | | 05.10.26 | |

| Стадия | Лист | Листов |
|---|---|---|
| П | 31 | 111 |

выпуск 05.10.2026 № 0516бс8858 · стр. 31 из 111

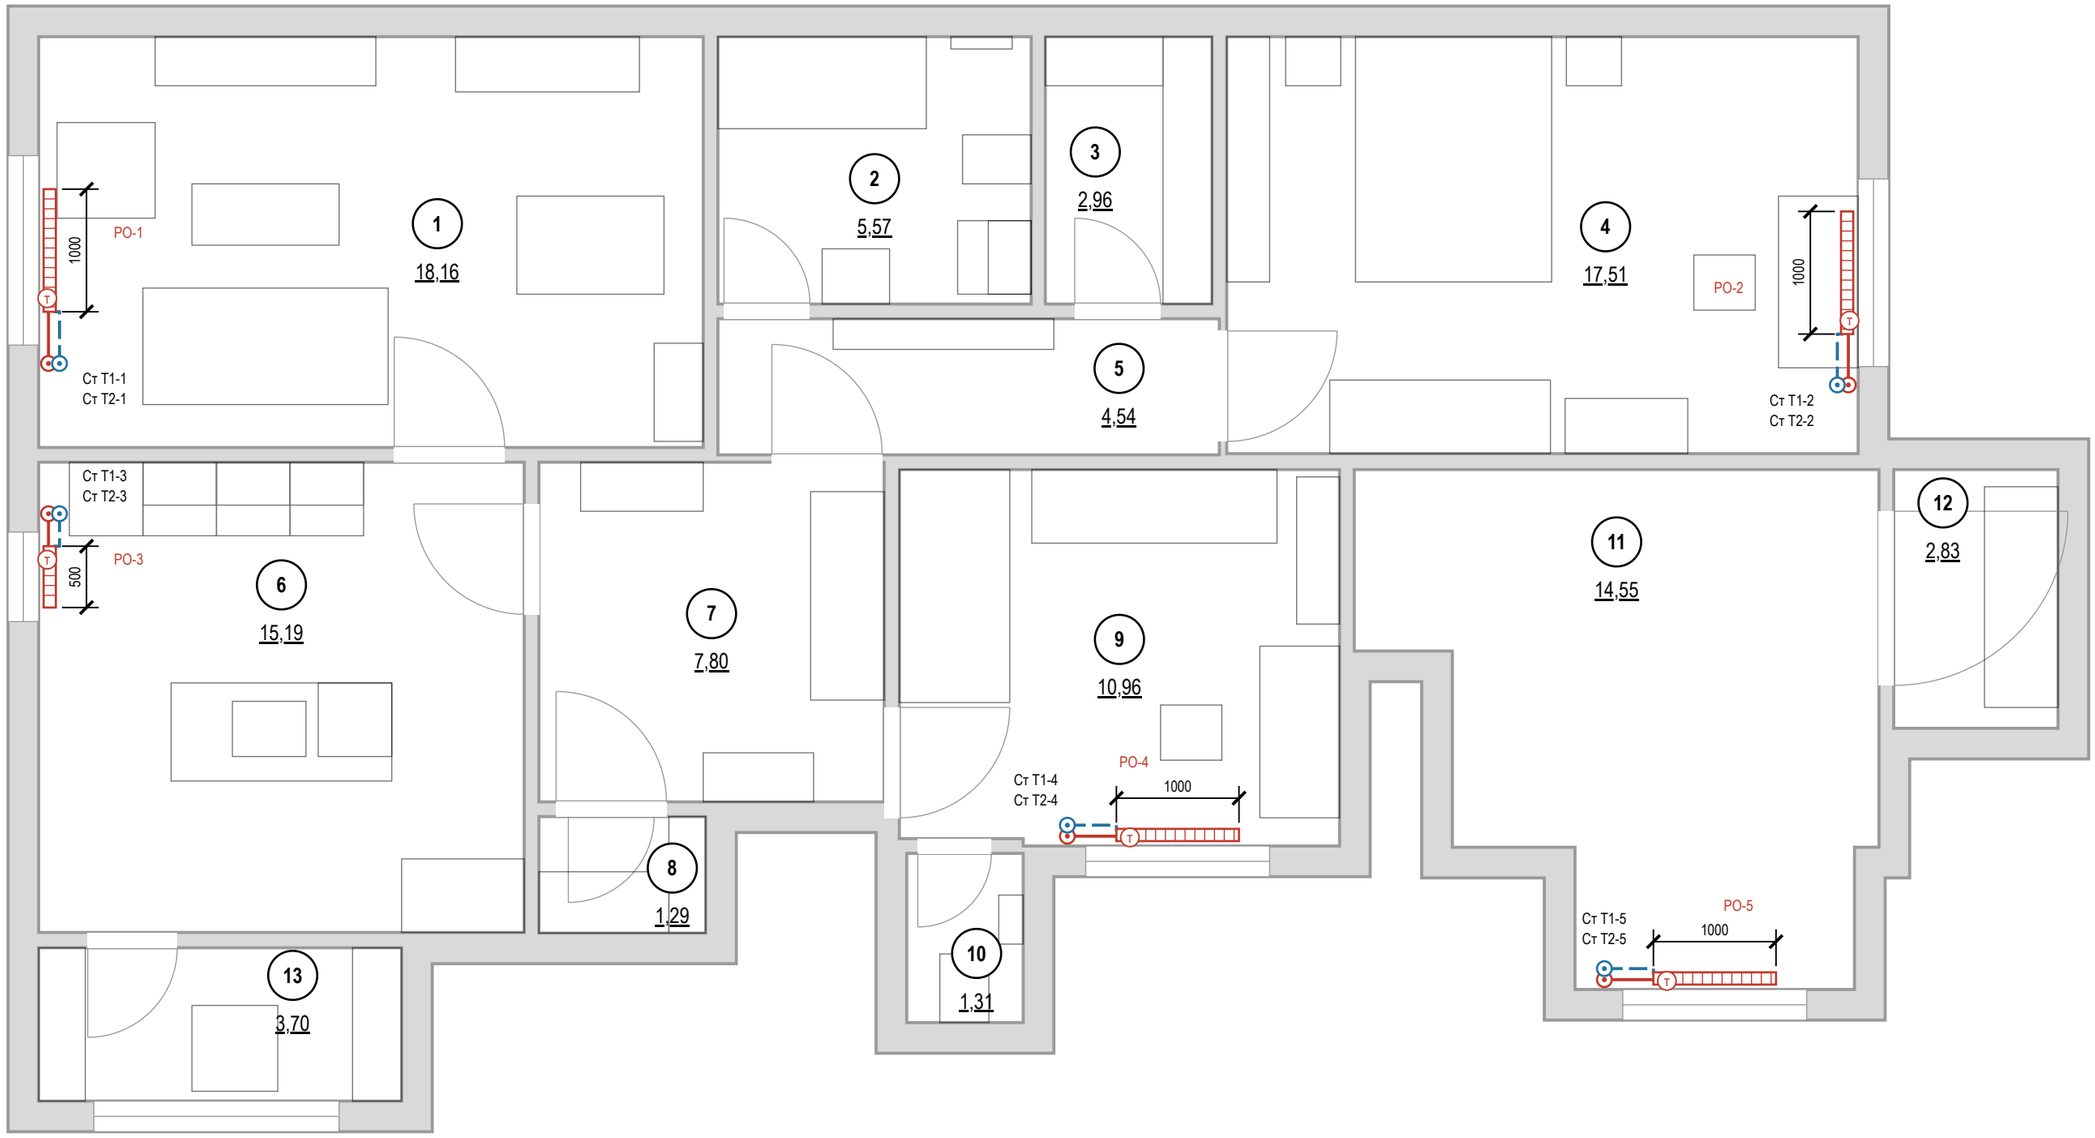


## Примечания

1. Расчёт системы отопления, теплопотерь и подбор приборов — проектная организация с допуском СРО; лист даёт места и привязки.
2. Тип, длина и мощность радиаторов — по теплотехническому расчёту; лист задаёт места, зазоры и подключение.
3. Радиаторы — под каждым окном жилых комнат и кухни, центр по оси проёма, длина 0,7 ширины окна (кратно 100); окончательно — по расчёту.
4. Зазоры радиатора: низ не менее 100 мм от чистого пола, верх не менее 100 мм до подоконника, 30–50 мм от стены до задней панели; центр по оси окна с допуском ±20 мм.
5. Радиаторы не закрывать глухими коробами и мебелью; перенос и замена приборов в многоквартирном доме — переустройство, согласование с управляющей организацией (ЖК РФ ст. 25–26); вынос на лоджию запрещён.
6. Трубы отопления через межквартирные стены не прокладывать (СП 51.13330.2011, п. 9.19); через перекрытия и перегородки — в гильзах.
7. Привязки приборов и подводок — по паспортам приобретённых радиаторов и клапанов, до черновых работ.
8. До закрытия отделкой трубопроводы отопления испытать гидростатическим давлением с оформлением акта (СП 73.13330.2016, 7.2–7.3).

| | | | | | |
|---|---|---|---|---|---|
| | | | | | Проект: Четырёхкомнатная квартира |
| | Лист | № док. | Подпись | Дата | |
| Дизайнер | Кырлан А.С. | | | 05.10.26 | План отопления |

| Стадия | Лист | Листов |
|---|---|---|
| П | 32 | 111 |


выпуск 05.10.2026 № 0516cc8858 · стр. 32 из 111

## Спецификация плинтусов






| Наименование | Помещения | Длина, м (с запасом) |
|---|---|---|
| Плинтус МДФ под окраску 80×16 мм, крепление к стене, окраска в цвет Tikkurila F497 | 1, 3, 4, 5, 6, 7, 8, 9, 11, 12 | 117 |
| Плинтус из керамогранита пола, подрезка 80 мм, верхняя кромка с запилом 45°, h = 80 мм, крепление к стене | 13 | 9 |

## Отметки по высоте

| | |
|---|---|
| **±0,000** | чистый пол пом. 1, 3–9, 11, 12; отсчёт высот |
| **−0,015** | чистый пол пом. 2, 10, ниже на 15 мм |
| **−0,030** | чистый пол пом. 13, ниже на 30 мм |
| **−0,170** | верх плиты — расчёт, не замер (задание на обмер) |
| **сущ. пол** | снимается до плиты; не замерен (задание на обмер) |

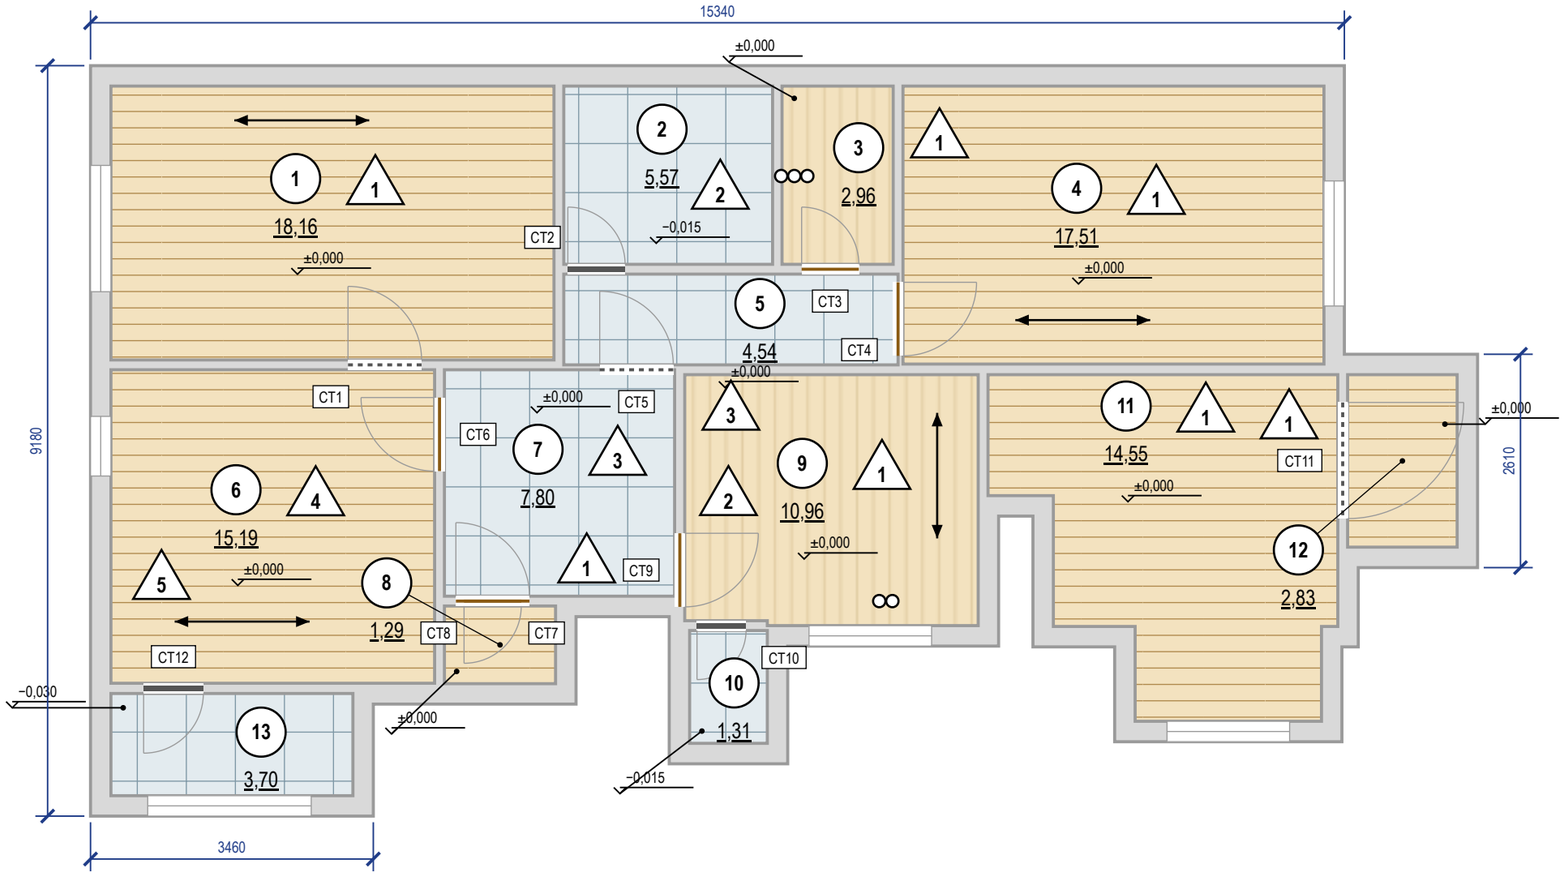


## Экспликация полов
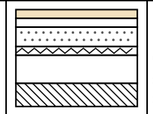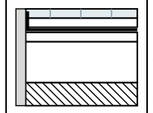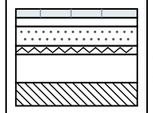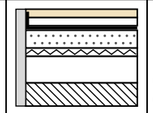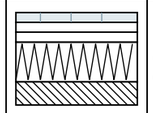
| Номер помещения | Тип пола | Схема пола | Данные элементов пола (наименование, толщина, основание), мм | Площадь, м² |
|---|---|---|---|---|
| 1, 3, 4, 8, 9, 11, 12 | 1 |  | Инженерная доска дуб на клею — 14<br>Клей паркетный МС-полимерный — 1<br>Стяжка ЦПС М300 (В22,5), фибра, по звукоизоляции — 55<br>Звукоизоляция — минплита 110 кг/м³ 20<br>Засыпка керамзитовая фр. 0–5, уплотнённая — 80<br>Плита перекрытия монолитная<br>Всего 170 мм; ЧП ±0,000, верх плиты −0,170 | 68,26 |
| 2, 10 | 2 |  | Керамогранит 600×600×10 — 10<br>Нагревательный мат в слое клея С2 TE S1 — 8<br>Гидроизоляция обмазочная, 2 слоя (заход на стены — по ведомости отделки) — 2<br>Сборное основание ГВЛВ 2×12,5 — 25<br>Засыпка керамзитовая сухая фр. 0–5 (в слое — выпуски К1) — 110<br>Плита перекрытия монолитная<br>Всего 155 мм; ЧП −0,015, верх плиты −0,170 | 6,88 |
| 5, 7 | 3 |  | Керамогранит 600×600×10 — 10<br>Клей плиточный С2 TE S1 — 5<br>Стяжка ЦПС М300 (В22,5), фибра, по звукоизоляции — 55<br>Звукоизоляция — минплита 110 кг/м³ 20<br>Засыпка керамзитовая фр. 0–5, уплотнённая — 80<br>Плита перекрытия монолитная<br>Всего 170 мм; ЧП ±0,000, верх плиты −0,170 | 12,34 |
| 6 | 4 |  | Инженерная доска дуб на клею — 14<br>Клей паркетный МС-полимерный — 1<br>Гидроизоляция полиуретановая, 2 слоя (зона мойки и острова) — 2<br>Стяжка ЦПС М300 (В22,5), фибра, по звукоизоляции — 53<br>Звукоизоляция — минплита 110 кг/м³ 20<br>Засыпка керамзитовая фр. 0–5, уплотнённая — 80<br>Плита перекрытия монолитная<br>Всего 170 мм; ЧП ±0,000, верх плиты −0,170 | 15,19 |
| 13 | 5 |  | Керамогранит 600×600×10 — 10<br>Клей плиточный С2 TE S1 (деформируемый) — 5<br>Сборное основание ГВЛВ 2×12,5 — 25<br>Пенополистирол экструзионный 2×50 100<br>Плита перекрытия монолитная<br>Всего 140 мм; ЧП −0,030, верх плиты −0,170 | 3,70 |
| | | | **Итого** | **106,37** |

## Примечания


1. За отметку ±0,000 принят чистый пол, не существующий (блок отметок). Площади — по чистым размерам помещений, м²; размеры — в мм.
2. Стык разнотипных покрытий — по оси дверного полотна (под полотном в закрытом положении); решение стыка — по ведомости стыков.
3. Пол санузлов ниже смежных помещений на 15 мм за счёт меньшей толщины стяжки (верх плиты общий — по экспликации полов); гидроизоляция по стяжке с заведением на стены не менее 200 мм (СП 29.13330.2011, п. 7.2), до облицовки — тест проливом и акт скрытых работ.
4. Выпуски канализации с уклоном и трассы водоснабжения — в слое засыпки под стяжкой (по экспликации полов); отметки, уклоны и прочистки — по листу разводки ВК 19.
5. Штучные покрытия (инженерная доска): направление — по стрелке; влажность основания по СМ не более 2,0 % (по ТУ изготовителя).
6. Ровность основания — просвет под 2-метровой рейкой не более 2 мм: пом. 1, 3, 4, 6, 8, 9, 11, 12 (инженерная доска), пом. 2, 5, 7, 10 (керамогранит); 3 мм: пом. 13 (керамогранит); проверить до укладки покрытия (СП 71.13330.2017, табл. 8.5).
7. Плавающая стяжка по звукоизоляции: демпферная (кромочная) лента по контуру помещения, у стояков и колонн — до верха чистого пола (СП 51.13330.2011, п. 9.11); плинтус крепится только к стене.
8. Сетка на плитке — условная, в размер формата; точка старта и раскладка — по листу раскладки плитки.
9. Пироги полов — по экспликации полов: слои сверху вниз, толщины в мм; гидроизоляция мокрых зон — в пироге и в ведомости отделки; схема пола — без масштаба.

| | | | | | |
|---|---|---|---|---|---|
| | | | | | Проект: Четырёхкомнатная квартира |
| | Лист | № док. | Подпись | Дата | План покрытий пола |
| Дизайнер | Кырлан А.С. | | | 05.10.26 | |


| Стадия | Лист | Листов |
|---|---|---|
| П | 33 | 111 |

выпуск 05.10.2026 № 05166c8858 · стр. 33 из 111


Фрагмент 1. Ванная комната (пом. 2). Пол 600×600, шов 2 мм, М 1:40

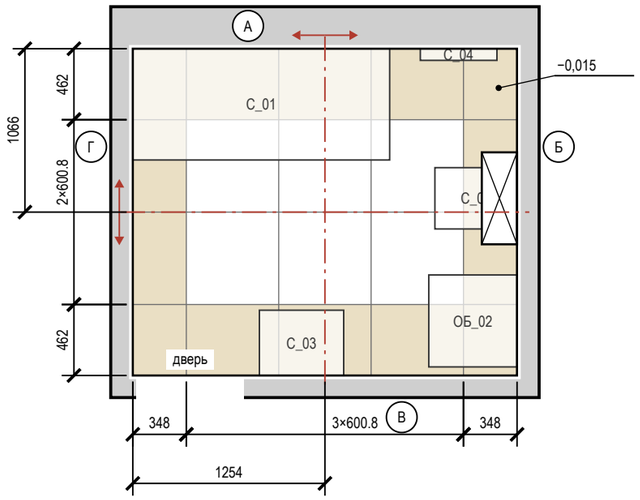



Фрагмент 2. Коридор (пом. 5). Пол 600×600, шов 2 мм, М 1:40

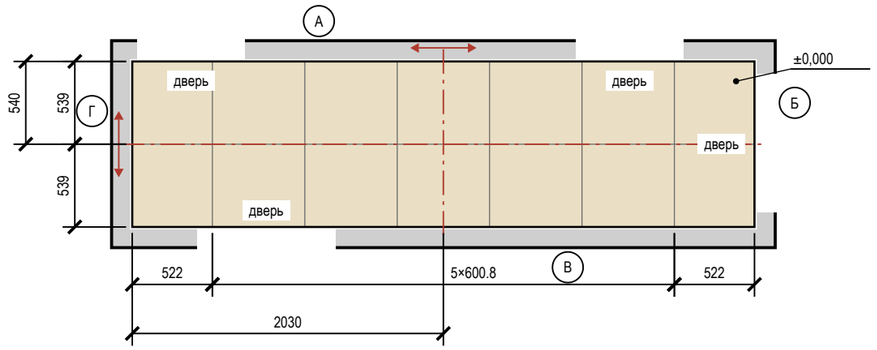


Фрагмент 3. Прихожая-коридор (пом. 7). Пол 600×600, шов 2 мм, М 1:40

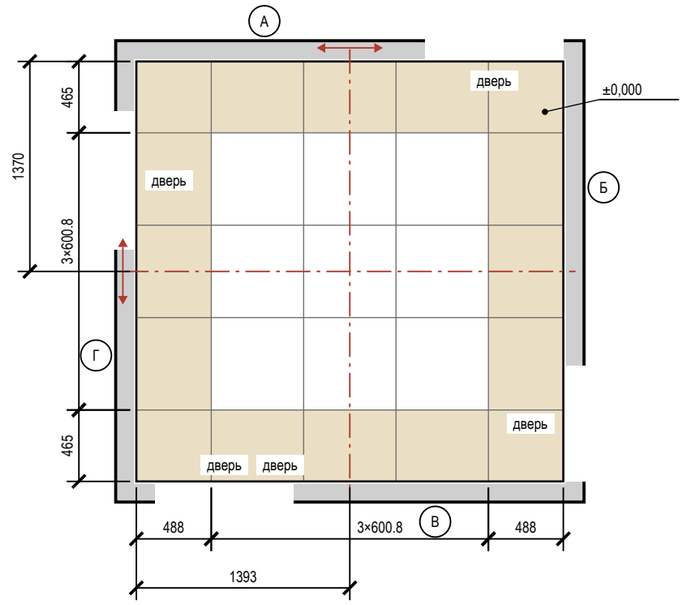


Фрагмент 4. Санузел (пом. 10). Пол 600×600, шов 2 мм, М 1:40

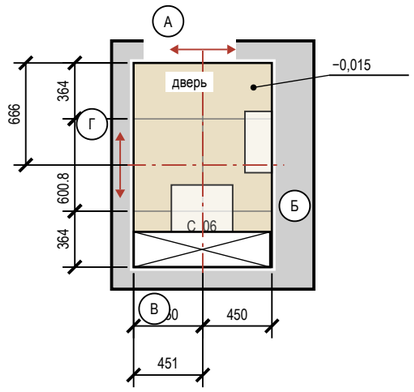


## Условные обозначения

- плитка целая; тонкая линия — шов
- плитка с подрезкой (размер — на цепочке)
- ось старта; стрелки — направление укладки
- сантехприбор: габарит, высота по практике
- короб инсталляции: плитка пола — до короба
- отметка чистого пола на полке выноски, м
- (А) обозначение стены А–Г (как на развёртках)

## Ведомость материалов

| Материал | Класс, код | Норма расхода | Кол-во |
|---|---|---|---|
| Затирка | CG2WA аналог: Mapei Ultracolor 133 | (a+b)/ab·шов·t·1,6 | 5,6 кг |
| Затирка | CG2WA | (a+b)/ab·шов·t·1,6 | 0,1 кг |
| Клей | C2 TE S1 аналог: Litokol K80 Eco | 1,5 кг/м²·мм, слой 5 | 425 кг (17 меш.) |
| Клей | C2 TE S1 | 1,5 кг/м²·мм, слой 5 | 10 кг (1 меш.) |
| Гидроизоляция | обмазочная, 2 слоя: пол, стены по периметру и зоны замачивания | по ТУ | 16,2 м² |
| Демпф. лента | по периметру пола из плитки | | 29,1 м |

## Ведомость плитки

| Помещение, поверхность | Плитка, код | Формат | Шов | S, м² | Целых | Подр. | С запасом |
|---|---|---|---|---|---|---|---|
| Ванная комната, пол | керамогранит матовый R10, тон J484 | 600.8×600.8 | 2 | 5,57 | 6 | 14 | 22 |
| Ванная комната, стены А–Г | керамогранит матовый, тон F497 | 600.8×600.8 | 2 | 21,66 | 23 | 67 | 100 |
| Ванная комната, короб инсталляции | керамогранит матовый, тон F497 | 600.8×600.8 | 2 | 1,36 | 1 | 6 | 8 |
| Коридор, пол | керамогранит матовый R10, тон V486 | 600.8×600.8 | 2 | 4,54 | 0 | 14 | 16 |
| Прихожая-коридор, пол | керамогранит матовый R10, тон V486 | 600.8×600.8 | 2 | 7,80 | 9 | 16 | 28 |
| Санузел, пол | керамогранит матовый R10, тон J484 | 600.8×600.8 | 2 | 1,31 | 0 | 6 | 7 |
| Санузел, стены А–Г | керамогранит матовый, тон F497 | 600.8×600.8 | 2 | 9,44 | 6 | 44 | 56 |
| Санузел, короб инсталляции | керамогранит матовый, тон F497 | 600.8×600.8 | 2 | 1,76 | 0 | 10 | 11 |
| Кухня, фартук (ст. А) | аналог: керамогранит матовый, тон F497 | 600.8×600.8 | 2 | 1,11 | 1 | 3 | 5 |
| **Итого 600.8×600.8** | | | | **54,54** | **46** | **180** | **253** |

## Примечания

1. Раскладка от чистовых размеров: стены санузлов теряют 10 + 5 + 9 = 24 мм на сторону (штукатурка, клей, плитка); подрезки — чистые, без шва.
2. Старт — от центра помещения (штрихпунктир, стрелки — направление укладки); размер старта — от чистовых стен Г и А.
3. Раскладка фартука «Кухня» — на листе «Раскладка плитки. Фартук кухни».
4. Количество: целые по раскладке + по одной на подрезку, запас 10 %; один артикул — одна партия и тон. Исключены поддон, короб, проёмы и места за коробом; S — по чистым граням: стены нетто = зона облицовки по ведомости отделки − место за коробом инсталляции 1,71 м² (плитку за коробом не кладут), короб — отдельной строкой.
5. Клей C2 TE S1 аналог: Litokol K80 Eco; C2 TE S1 (ГОСТ Р 56387-2018), затирка CG2WA аналог: Mapei Ultracolor 133; CG2WA; расход — по ТУ выбранной марки.
6. Гидроизоляция: пол и стены 200 мм от ЧП; над ванной — до 2100 и 300 мм за борт (см. развёртки); акт скрытых работ, пролив 24 ч.
7. Швы пола совмещены со швами стены А; по периметру — демпферная лента.
8. Отметка чистого пола −0,015, порог 15 мм; стык с соседним покрытием — по оси полотна двери.

| | | | | |
|---|---|---|---|---|
| | | | | |
| | Лист | № док. | Подпись | Дата |
| Дизайнер | Кырлан А.С. | | | 05.10.26 |
| | | | | |


Проект: Четырёхкомнатная квартира

Раскладка плитки. Планы полов

| Стадия | Лист | Листов |
|---|---|---|
| П | 34 | 111 |

выпуск 05.10.2026 № 05166c8858 · стр. 34 из 111

**Фрагмент 1. Кухня (пом. 6), фартук, стена А. 600×600, шов 2 мм, М 1:20**

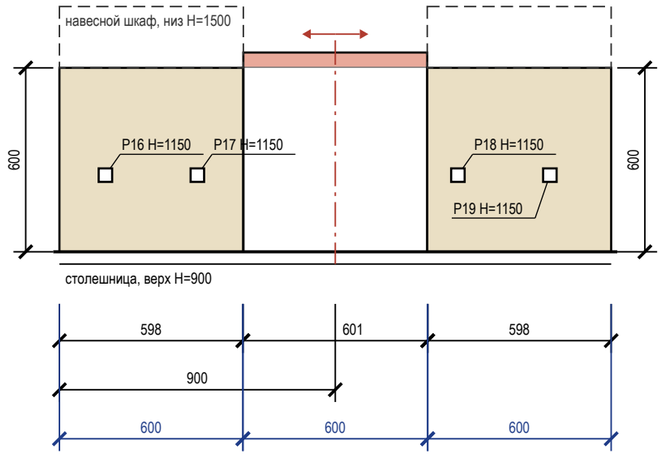


## Условные обозначения

- плитка целая; тонкая линия — шов
- плитка с подрезкой (размер — на цепочке)
- ось старта; стрелки — направление укладки
- электроточка: марка и Н — по листам ЭОМ
- столешница (верх)
- навесной шкаф над фартуком

## Подсчёт плитки

| Поверхность | Формат | S, м² | Целых | Подр. | С запасом |
|---|---|---|---|---|---|
| Кухня, фартук (ст. А) | 600×600 | 1,11 | 1 | 3 | 5 |

## Сдвиг розеток фартука под раскладку

| Точка (ЭОМ) | Проект: от угла / Н | Под раскладку: от угла / Н | Сдвиг, мм |
|---|---|---|---|
| Р16 | 150 / 1150 | 297 / 1200 | +147 от шва; Н +50 ось ряда |
| Р17 | 450 / 1150 | 599 / 1200 | +149 на шов; Н +50 ось ряда |
| Р18 | 1300 / 1150 | 1201 / 1200 | −99 на шов; Н +50 ось ряда |
| Р19 | 1600 / 1150 | 1503 / 1200 | −97 от шва; Н +50 ось ряда |

## Примечания

1. Фартук, Кухня: 600×600 горизонтально, шов 2 мм; зоны 600 мм — 900…1500, 600 мм — 900…1550, 600 мм — 900…1500 (от столешницы до низа навесного шкафа, без шкафа — 650 мм). Старт от центра участка, подрезки 598 мм. Площадь 1,11 м² — как в ведомости отделки.
2. Фартук — после монтажа столешницы, низ на 2–3 мм выше неё, шов со столешницей — санитарный герметик; навесные шкафы — после фартука. Торцы у пенала и стены — профиль или запил 45°.
3. Фартук, Кухня: в зоне до отм. 1550 верхний ряд подрезан 47 мм — меньше 1/3 плитки; полоса прикрыта корпусом навесного модуля и на виду не остаётся. Раскладкой не снимается: убрать подрезку можно, только выровняв низ этого модуля с соседними (1500 мм) — решение мебельщика.
4. Розетки из таблицы переносятся до черновой электрики: по высоте — на ось ряда плитки, от вертикального шва крупной плитки — не ближе 60 мм. Привязка — от левого края фартука на развёртке.
5. Клей, затирка и итог по форматам — в ведомостях листа «Раскладка плитки. Планы полов».

| | | | | | |
|---|---|---|---|---|---|
| | | | | | Проект: Четырёхкомнатная квартира |
| | Лист | № док. | Подпись | Дата | Раскладка плитки. Фартук кухни |
| Дизайнер | Кырлан А.С. | | | 05.10.26 | |

| Стадия | Лист | Листов |
|---|---|---|
| П | 35 | 111 |

выпуск 05.10.2026 № 0516c8858 · стр. 35 из 111



| | | | | | |
|---|---|---|---|---|---|
| | | | | | Проект: Четырёхкомнатная квартира |
| | Лист | № док. | Подпись | Дата | |
| Дизайнер | Кырлан А.С. | | | 05.10.26 | Визуализация. Вид сверху |

| Стадия | Лист | Листов |
|---|---|---|
| П | 36 | 111 |

выпуск 05.10.2026 № 0516c8858 · стр. 36 из 111



| | | | | | |
|---|---|---|---|---|---|
| | | | | | Проект: Четырёхкомнатная квартира |
| | Лист | № док. | Подпись | Дата | |
| Дизайнер | Кырлан А.С. | | | 05.10.26 | Визуализация: Зал |

| Стадия | Лист | Листов |
|---|---|---|
| П | 37 | 111 |

выпуск 05.10.2026 № 0516c8858 · стр. 37 из 111



| | | | | | |
|---|---|---|---|---|---|
| | | | | | Проект: Четырёхкомнатная квартира |
| | Лист | № док. | Подпись | Дата | |
| Дизайнер | Кырлан А.С. | | | 05.10.26 | Визуализация: Зал |
| | | | | | Стадия: П; Лист: 38; Листов: 111 |

выпуск 05.10.2026 № 05166c8858 · стр. 38 из 111



| | | | | | |
|---|---|---|---|---|---|
| | | | | | Проект: Четырёхкомнатная квартира |
| | Лист | № док. | Подпись | Дата | |
| Дизайнер | Кырлан А.С. | | | 05.10.26 | Визуализация: Зал |
| | | | | | Стадия: П; Лист: 39; Листов: 111 |

выпуск 05.10.2026 № 0516c8858 · стр. 39 из 111




| | | | | | |
|---|---|---|---|---|---|
| | | | | | Проект: Четырёхкомнатная квартира |
| | Лист | № док. | Подпись | Дата | |
| Дизайнер | Кырлан А.С. | | | 05.10.26 | Визуализация: Зал |


| Стадия | Лист | Листов |
|---|---|---|
| П | 40 | 111 |

выпуск 05.10.2026 № 0516cc8858 · стр. 40 из 111

## Развёртка стены А

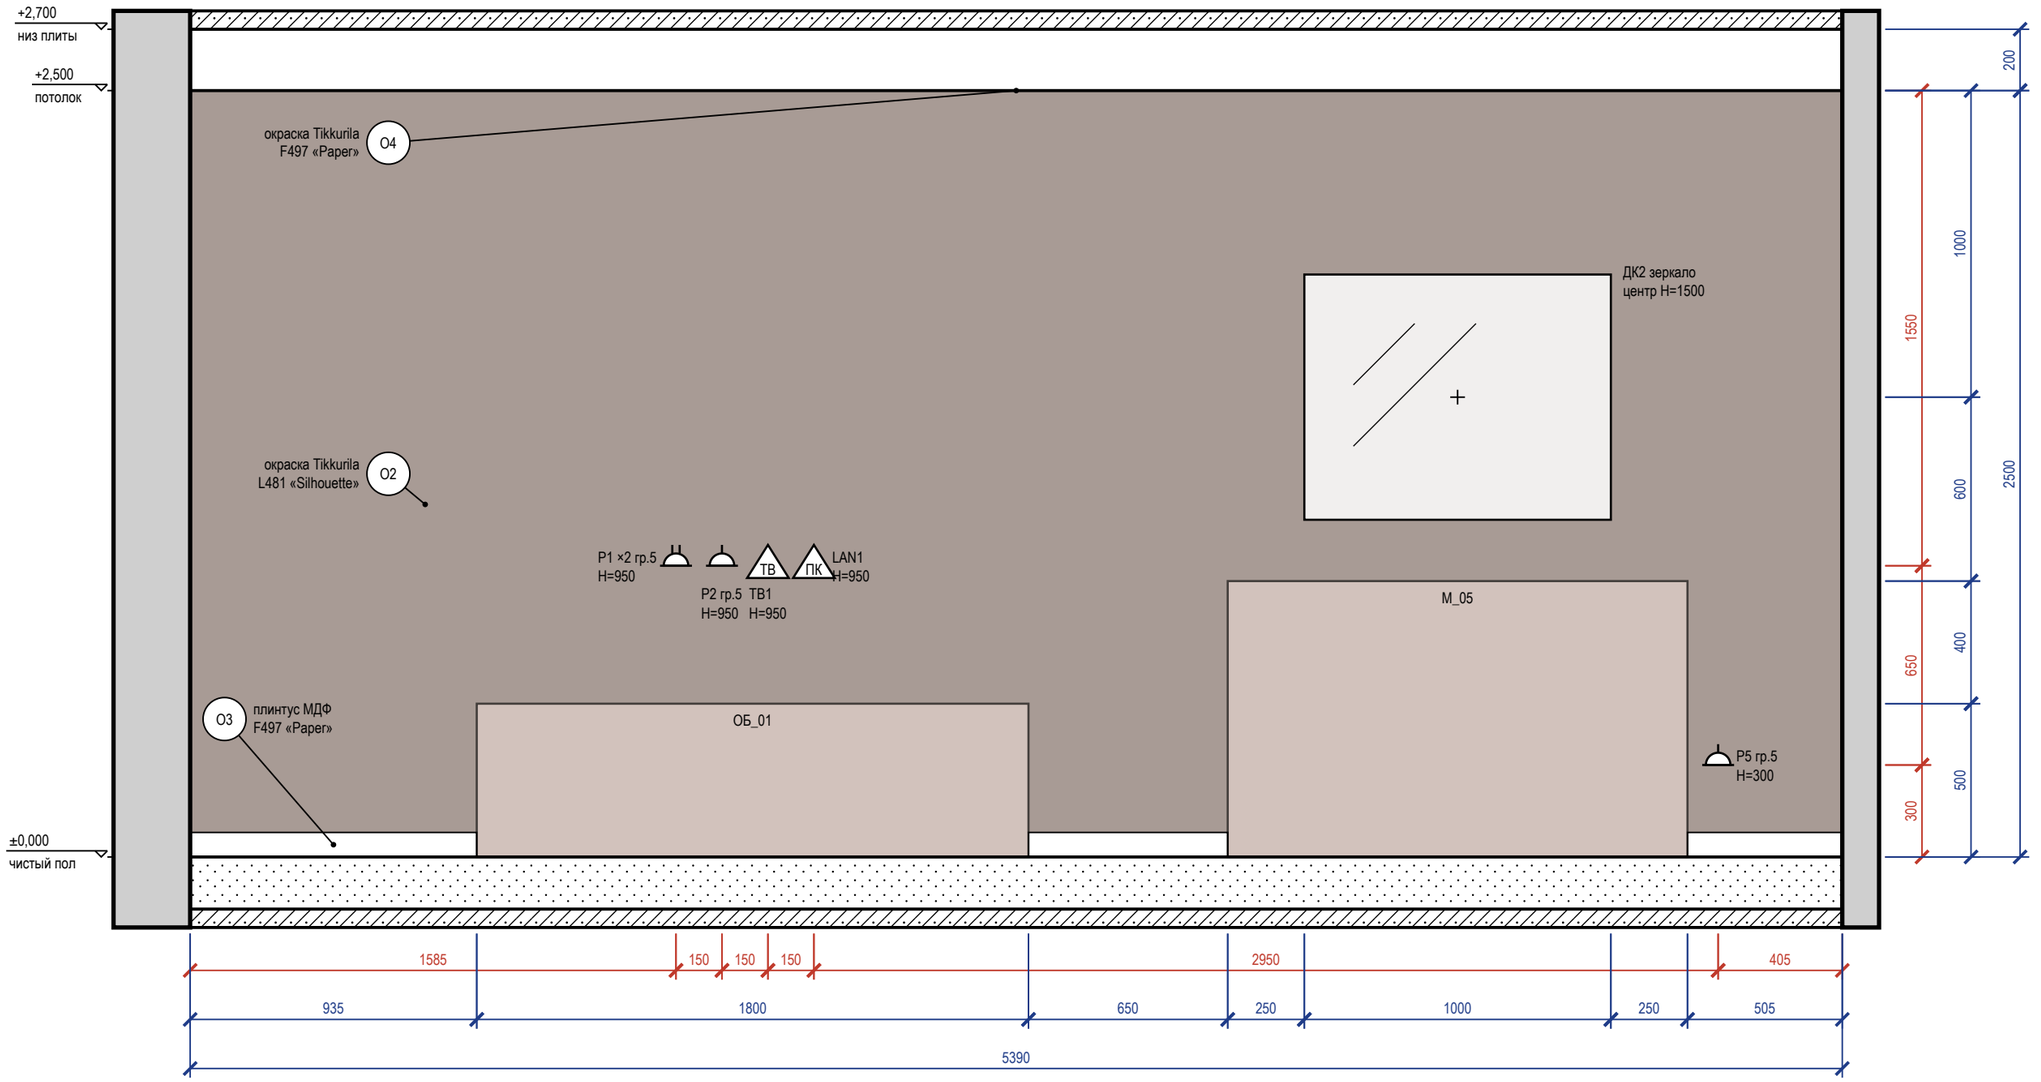



### Схема развёрток (М 1:100)

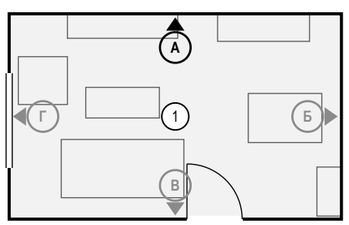


### Ведомость отделки (на листе)

| Марка | Поверхность | Материал, изделие | Цвет, код | Кол. |
|---|---|---|---|---|
| O2 | акцентная стена | окраска, Tikkurila Optiva 5 Matt, аналог: интерьерная краска, класс 2 по EN 13300, глубокоматовая/матовая, база C, матовая, подготовка К3 | Tikkurila L481 «Silhouette» | 13,5 м² |
| O3 | плинтус | плинтус МДФ, h 80 мм, аналог: плинтус МДФ под окраску 80×16 мм, полуглянцевая | Tikkurila F497 «Paper» | 2,1 м |
| O4 | потолок | окраска, Tikkurila Anti-Reflex 2, глубокоматовая, подготовка Q3 | Tikkurila F497 «Paper» | 18,2 м² |

Визуализация этой стены — лист 37

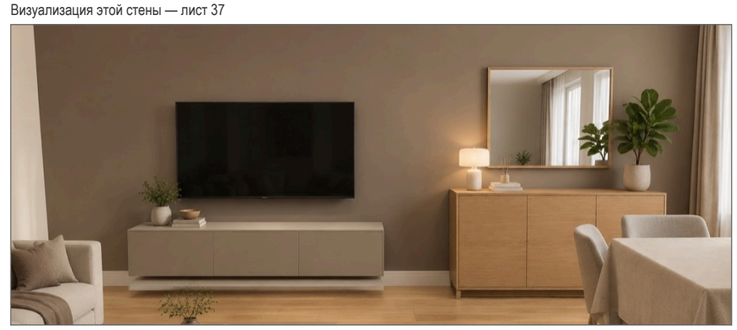

### Примечания

1. Размеры — в мм от чистовых поверхностей стен; условные обозначения и общие указания — лист 2.
2. Картины и зеркала крепить к основанию по паспорту изделия (закладные и анкеры — в перечне скрытых работ); крест — ось центра предмета.
3. Потолок на развёртках — по нижнему уровню У1; другие уровни потолка помещения: У2 +2,600.

| | | | | |
|---|---|---|---|---|
| | | | | |
| | | | | |
| | Лист | № док. | Подпись | Дата |
| Дизайнер | Кырлан А.С. | | | 05.10.26 |
| | | | | |


Проект: Четырёхкомнатная квартира

Развёртка стены А. Зал (пом. 1)


| Стадия | Лист | Листов |
|---|---|---|
| П | 41 | 111 |

выпуск 05.10.2026 № 05166c8858 · стр. 41 из 111

## Развёртка стены Б

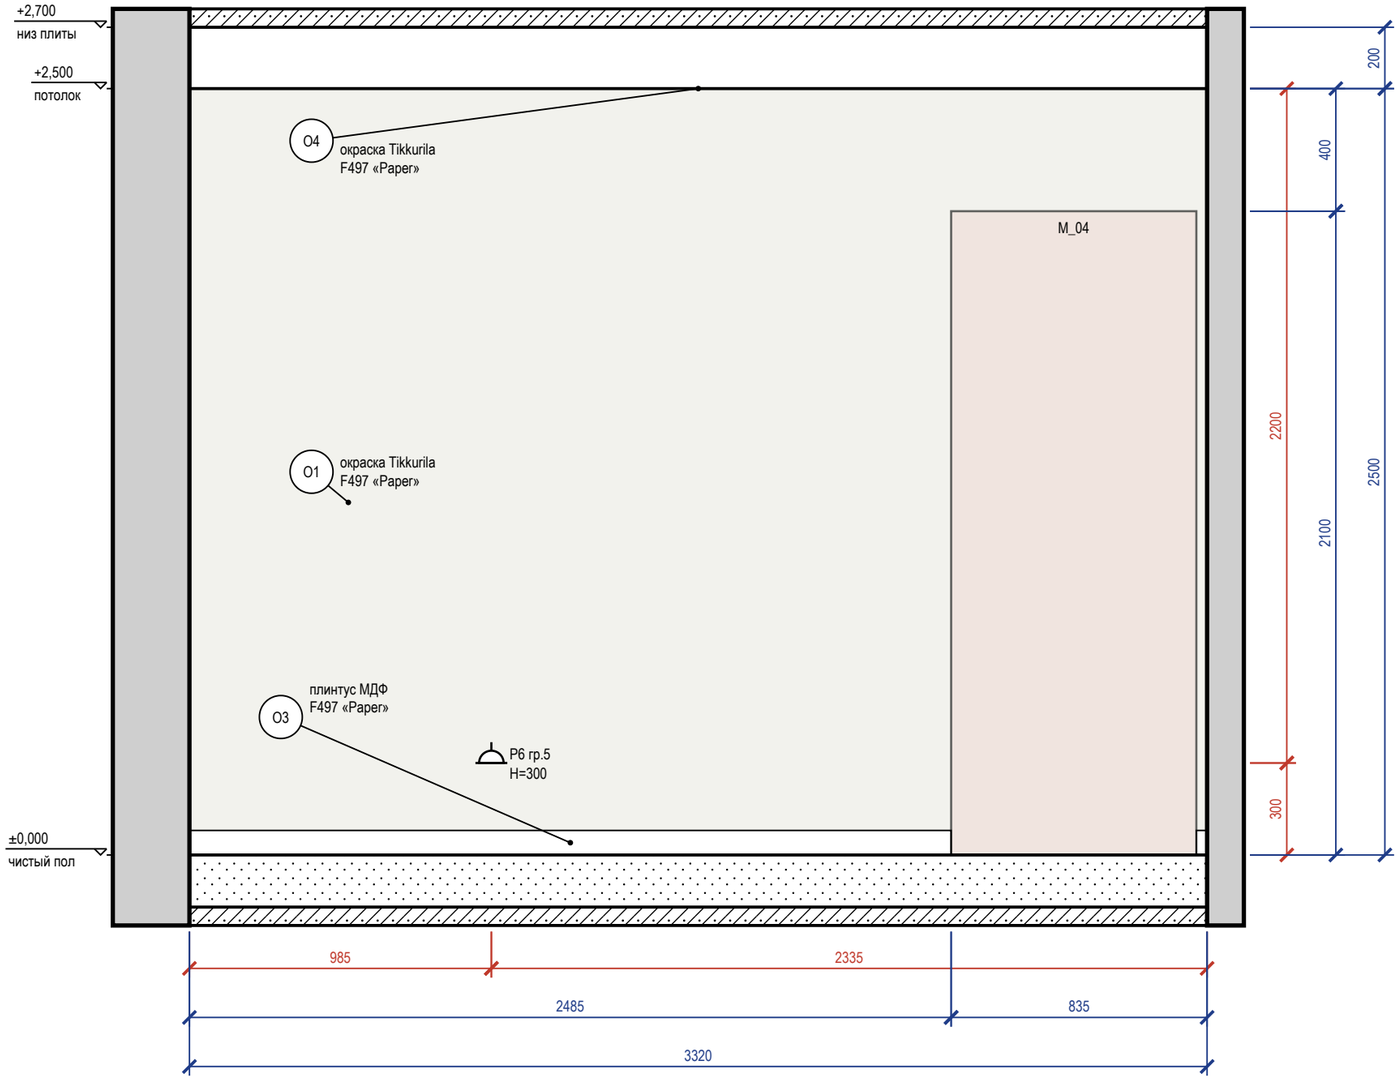


## Схема развёрток (М 1:100)

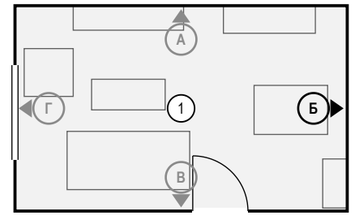


## Ведомость отделки (на листе)

| Марка | Поверхность | Материал, изделие | Цвет, код | Кол. |
|---|---|---|---|---|
| О1 | стены | окраска, Tikkurila Optiva 5 Matt, матовая, подготовка К3 | Tikkurila F497 «Paperг» | 8,3 м² |
| О3 | плинтус | плинтус МДФ, h 80 мм, аналог: плинтус МДФ под окраску 80×16 мм, полуглянцевая | Tikkurila F497 «Paperг» | 2,5 м |
| О4 | потолок | окраска, Tikkurila Anti-Reflex 2, глубокоматовая, подготовка Q3 | Tikkurila F497 «Paperг» | 18,2 м² |

Визуализация этой стены — лист 38




## Примечания

1. Размеры — в мм от чистовых поверхностей стен; условные обозначения и общие указания — лист 2.
2. Потолок на развёртках — по нижнему уровню У1; другие уровни потолка помещения: У2 +2,600.


| | | | | | |
|---|---|---|---|---|---|
| | | | | | Проект: Четырёхкомнатная квартира |
| | Лист | № док. | Подпись | Дата | |
| Дизайнер | Кырлан А.С. | | | 05.10.26 | Развёртка стены Б. Зал (пом. 1) |
| | | | | | Стадия: П; Лист: 42; Листов: 111 |

выпуск 05.10.2026 № 0516c8858 · стр. 42 из 111

## Развёртка стены В

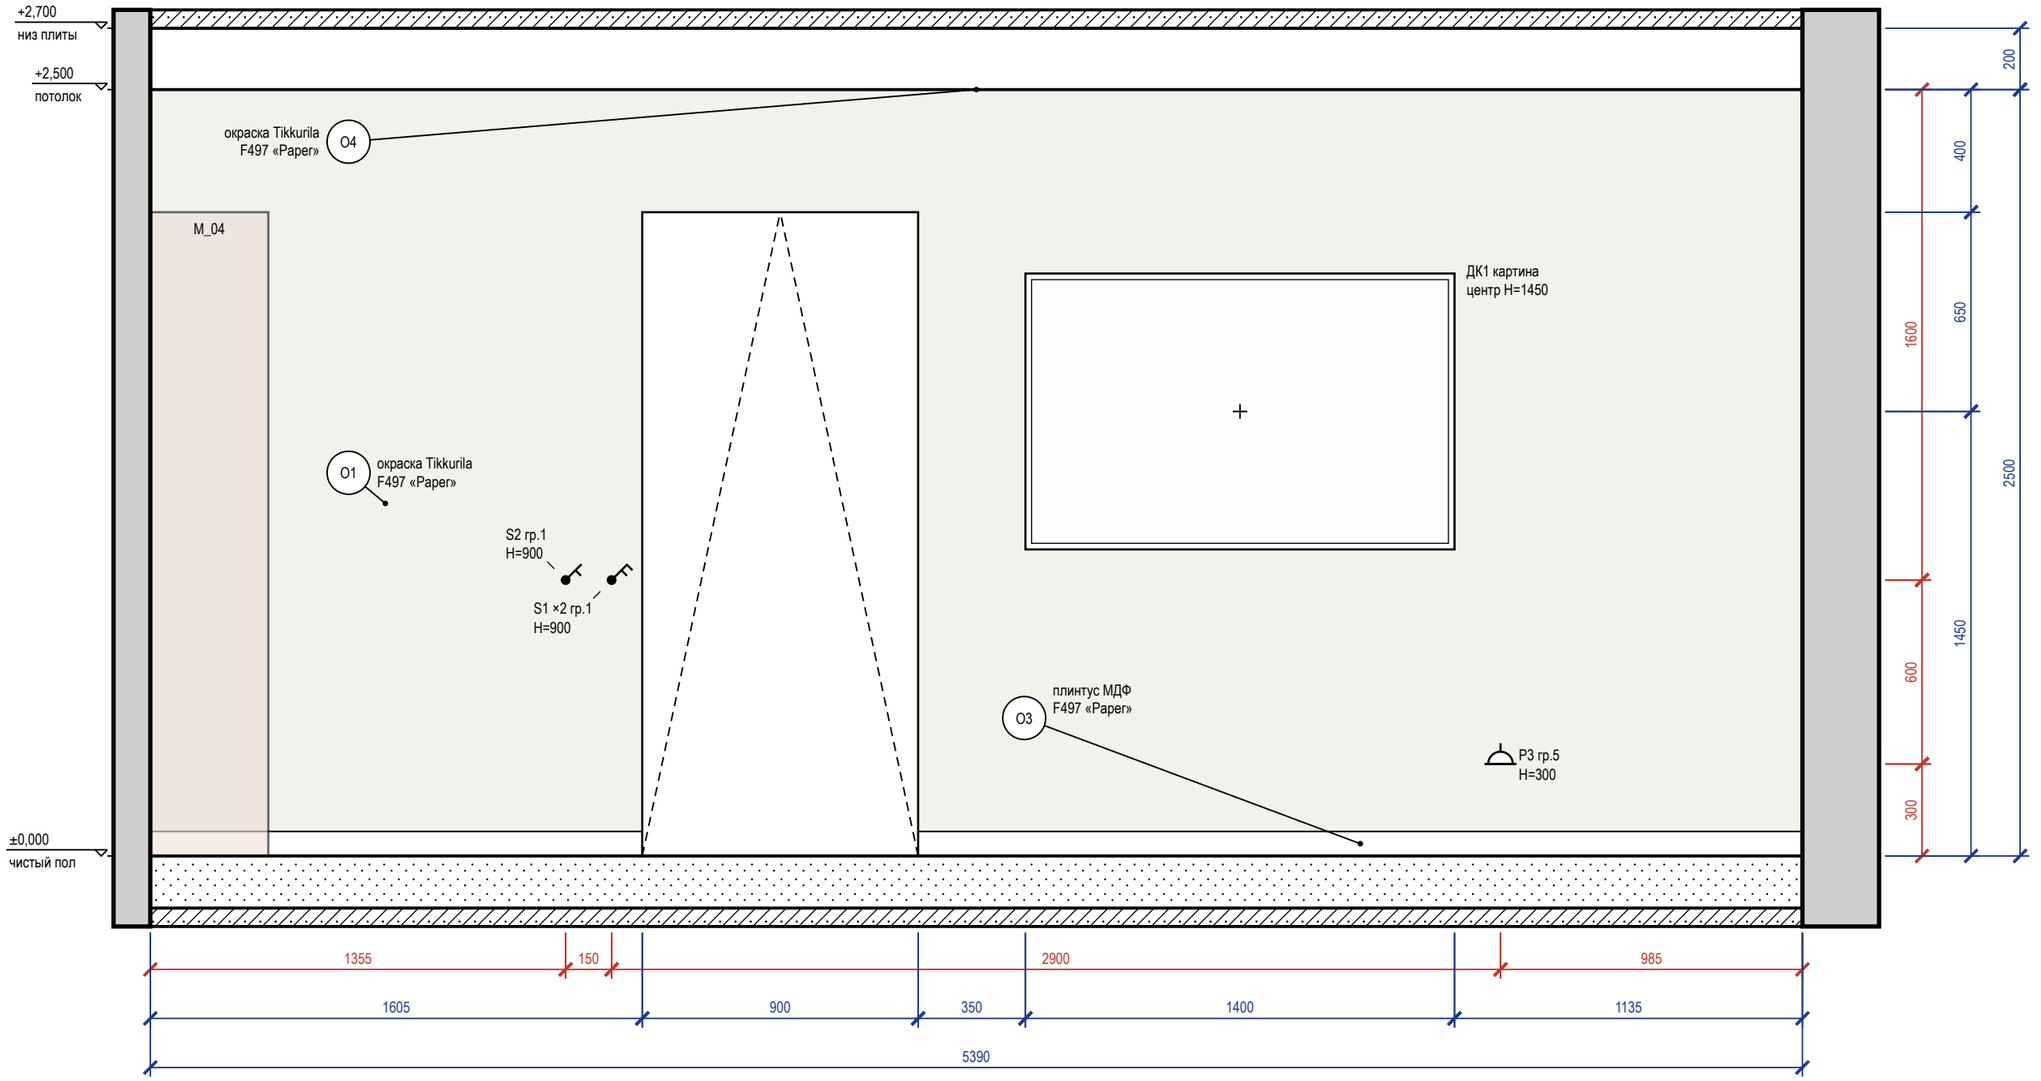



### Схема развёрток (М 1:100)

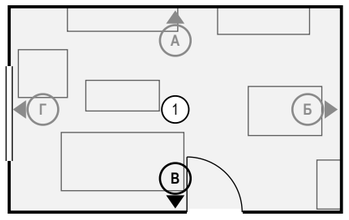


### Ведомость отделки (на листе)

| Марка | Поверхность | Материал, изделие | Цвет, код | Кол. |
|---|---|---|---|---|
| О1 | стены | окраска, Tikkurila Optiva 5 Matt, матовая, подготовка К3 | Tikkurila F497 «Paperг» | 11,6 м² |
| О3 | плинтус | плинтус МДФ, h 80 мм, аналог: плинтус МДФ под окраску 80×16 мм, полуглянцевая | Tikkurila F497 «Paperг» | 4,5 м |
| О4 | потолок | окраска, Tikkurila Anti-Reflex 2, глубокоматовая, подготовка Q3 | Tikkurila F497 «Paperг» | 18,2 м² |

Визуализация этой стены — лист 39

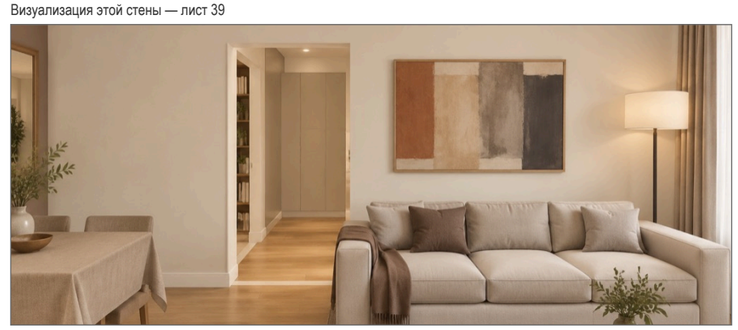


### Примечания

1. Размеры — в мм от чистовых поверхностей стен; условные обозначения и общие указания — лист 2.
2. Картины и зеркала крепить к основанию по паспорту изделия (закладные и анкеры — в перечне скрытых работ); крест — ось центра предмета.
3. Потолок на развёртках — по нижнему уровню У1; другие уровни потолка помещения: У2 +2,600.


| | | | | | |
|---|---|---|---|---|---|
| | | | | | Проект: Четырёхкомнатная квартира |
| | Лист | № док. | Подпись | Дата | |
| Дизайнер | Кырлан А.С. | | | 05.10.26 | Развёртка стены В. Зал (пом. 1) |
| | | | | | Стадия: П; Лист: 43; Листов: 111 |

выпуск 05.10.2026 № 05166c8858 · стр. 43 из 111

## Развёртка стены Г

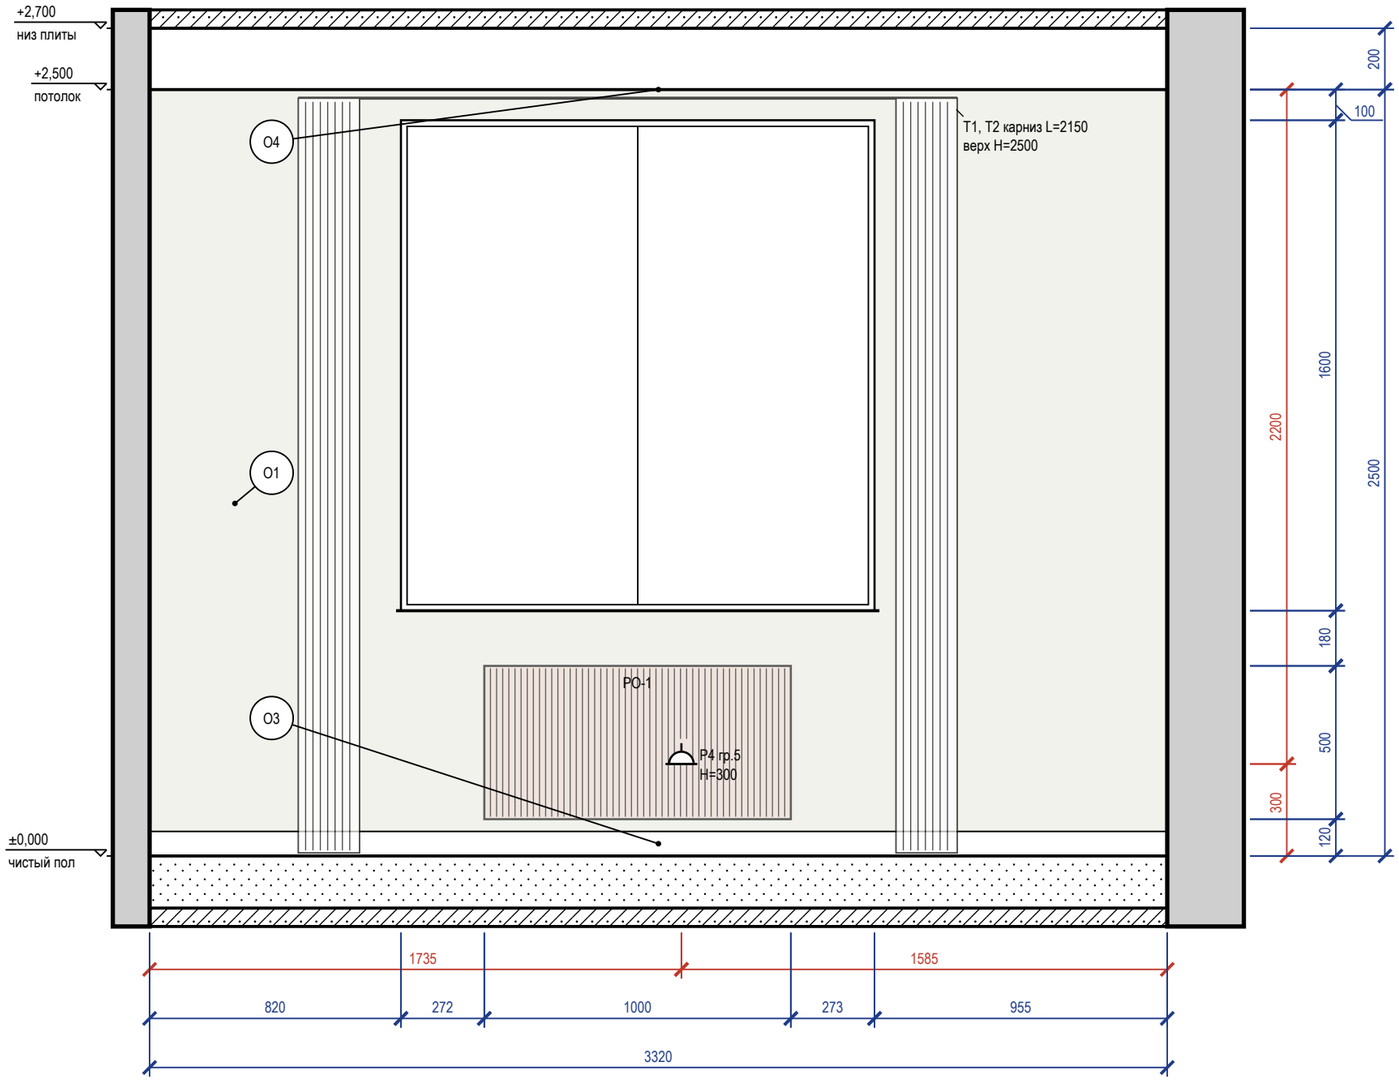


## Схема развёрток (М 1:100)

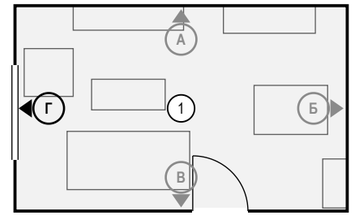


## Ведомость отделки (на листе)

| Марка | Поверхность | Материал, изделие | Цвет, код | Кол. |
|---|---|---|---|---|
| О1 | стены | окраска, Tikkurila Optiva 5 Matt, матовая, подготовка К3 | Tikkurila F497 «Paper» | 5,8 м² |
| О3 | плинтус | плинтус МДФ, h 80 мм, аналог: плинтус МДФ под окраску 80×16 мм, полуглянцевая | Tikkurila F497 «Paper» | 3,3 м |
| О4 | потолок | окраска, Tikkurila Anti-Reflex 2, глубокоматовая, подготовка Q3 | Tikkurila F497 «Paper» | 18,2 м² |

Визуализация этой стены — лист 40



### Примечания

1. Размеры — в мм от чистовых поверхностей стен; условные обозначения и общие указания — лист 2.
2. Карнизы (шины) — по ведомости текстиля декоратора; длина L и верх H — по развёртке, крепление — до окраски потолка.
3. Потолок на развёртках — по нижнему уровню У1; другие уровни потолка помещения: У2 +2,600.
4. Линии узора (швы плитки, складки штор, рёбра радиаторов) прерываются у знаков и выносок — просвет между линиями не менее 0,7 мм.

| | | | | | | |
|---|---|---|---|---|---|---|
| | | | | | Проект: Четырёхкомнатная квартира | |
| | Лист | № док. | Подпись | Дата | Развёртка стены Г. Зал (пом. 1) | Стадия / Лист / Листов |
| Дизайнер | Кырлан А.С. | | | 05.10.26 | | П / 44 / 111 |


выпуск 05.10.2026 № 05166c8858 · стр. 44 из 111




| | | | | | | |
|---|---|---|---|---|---|---|
| | | | | | Проект: Четырёхкомнатная квартира | |
| | Лист | № док. | Подпись | Дата | | |
| Дизайнер | Кырлан А.С. | | | 05.10.26 | Визуализация: Ванная комната | Стадия / Лист / Листов |
| | | | | | | П / 45 / 111 |

выпуск 05.10.2026 № 0516c8858 · стр. 45 из 111


## Развёртка стены А

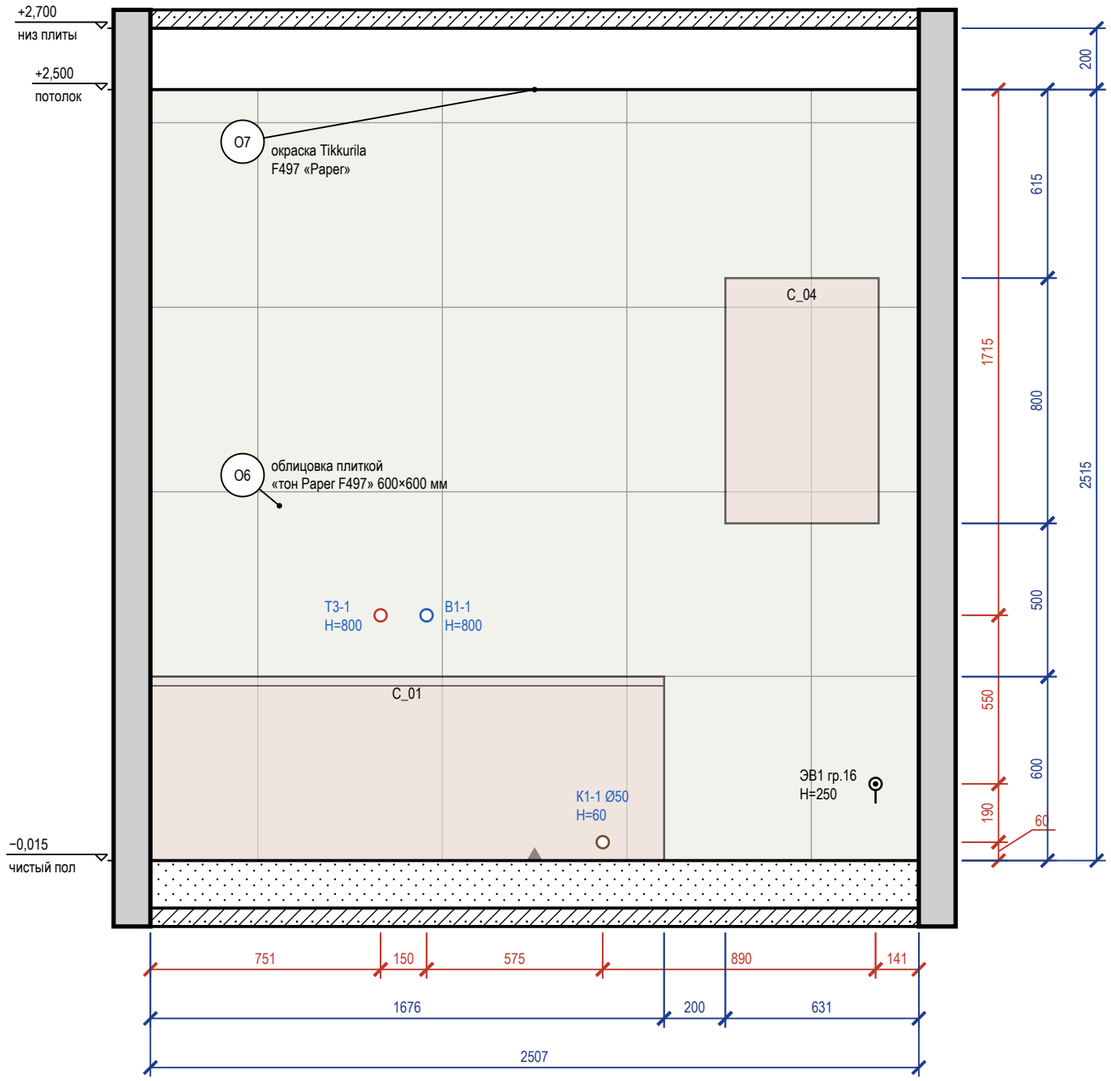


## Развёртка стены Б

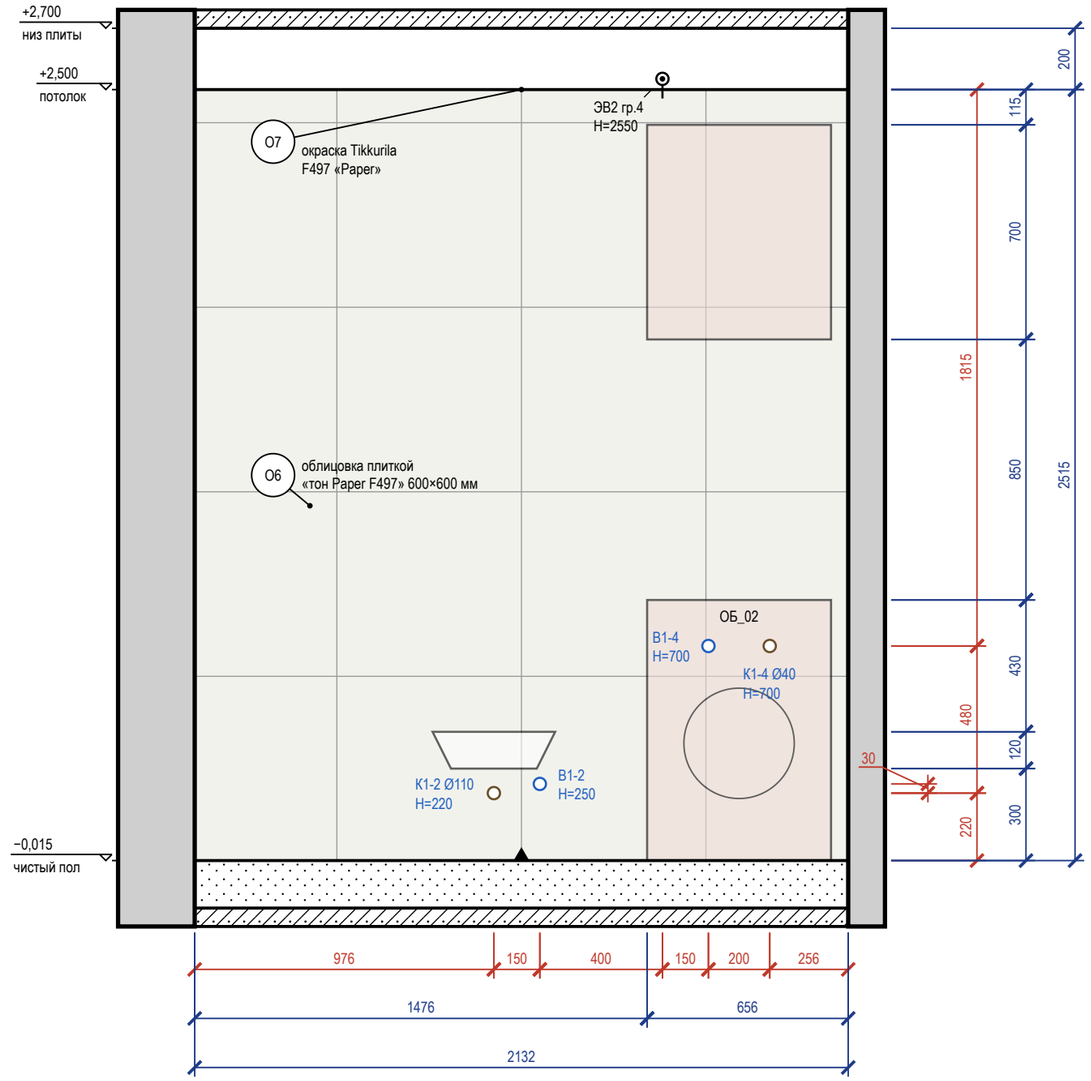



### Схема развёрток (М 1:100)

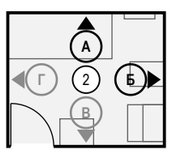


### Ведомость отделки (на листе)

| Марка | Поверхность | Материал, изделие | Цвет, код | Кол. |
|---|---|---|---|---|
| О6 | стены | облицовка плиткой, 600×600×9 мм, аналог: керамогранит матовый, тон F497, затирка CG2WA | #F1F1EC «тон Paper F497» | 11,7 м² |
| О7 | потолок | окраска, Tikkurila Luja 7, матовая, подготовка Q3 | Tikkurila F497 «Paper» | 5,6 м² |

Визуализация этой стены — лист 45

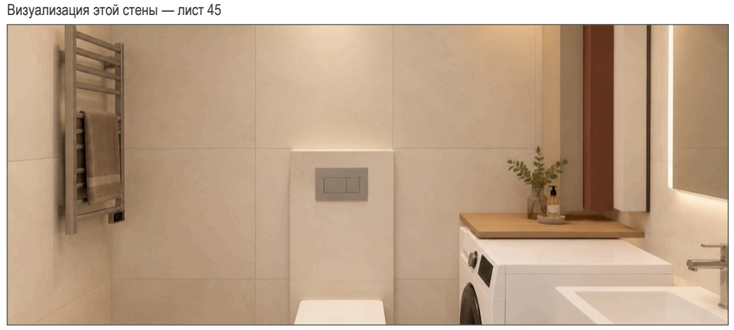

### Примечания


1. Размеры — в мм от чистовых поверхностей стен; условные обозначения и общие указания — лист 2.
2. Схема мебели, приборов и декора не является технической документацией для производства мебели; габариты — по паспортам изделий.
3. Облицовка — по сетке швов 2 мм, раскладка от оси стены (треугольник у пола); подрезки — по листу раскладки плитки.
4. Гидроизоляция в 2 слоя, заход на стены 200 мм, в зоне душа — 2100 мм — до облицовки, с актом скрытых работ и тестом проливом (узел — на листе узлов).

| | | | | | |
|---|---|---|---|---|---|
| | | | | | Проект: Четырёхкомнатная квартира |
| | Лист | № док. | Подпись | Дата | Развёртки стен А, Б. Ванная комната (пом. 2) |
| Дизайнер | Кырлан А.С. | | | 05.10.26 | |


| Стадия | Лист | Листов |
|---|---|---|
| П | 46 | 111 |

выпуск 05.10.2026 № 05166c8858 · стр. 46 из 111


## Развёртка стены В

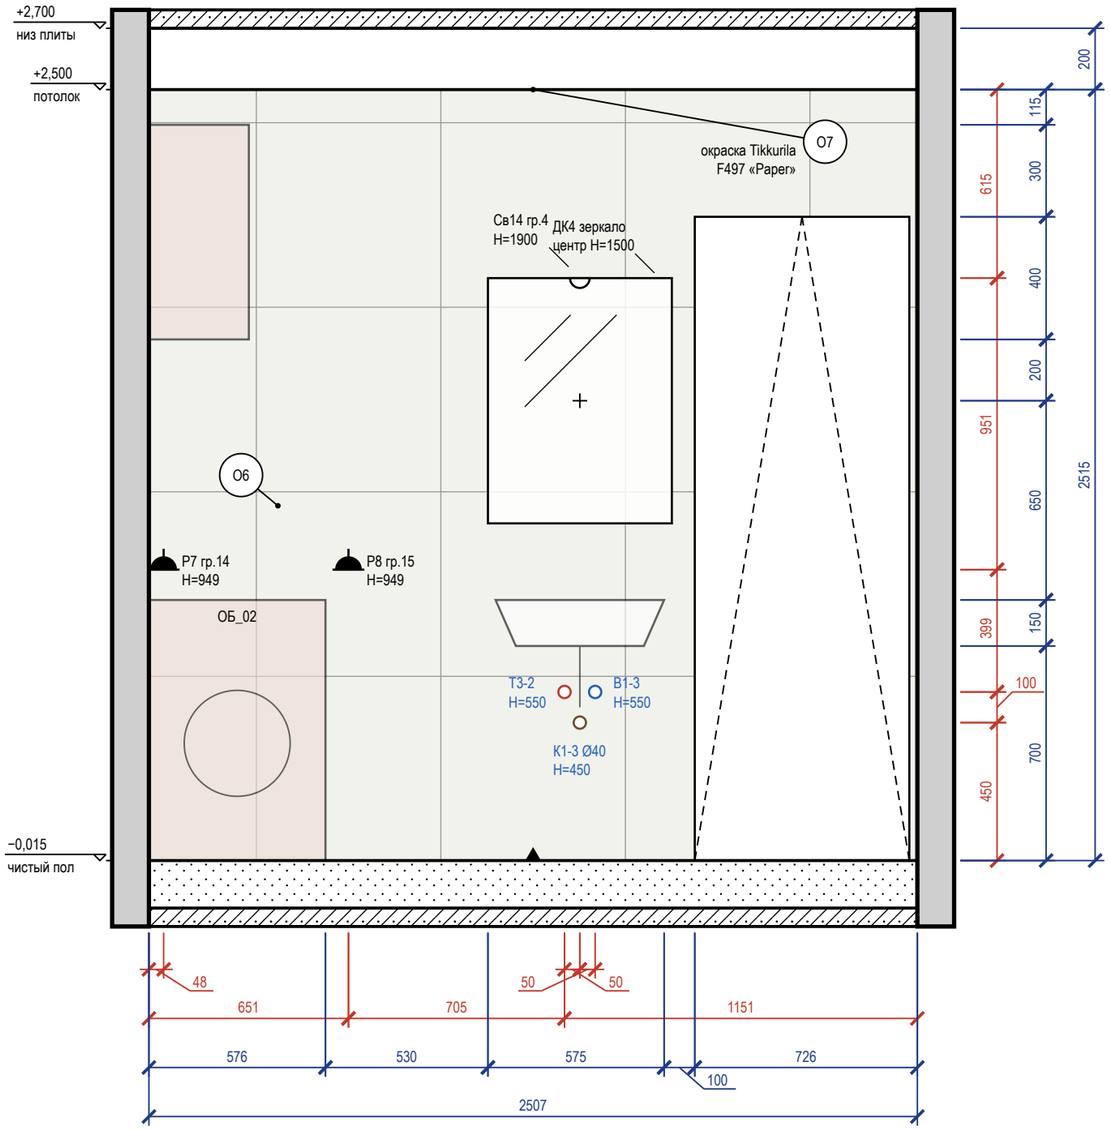


## Развёртка стены Г

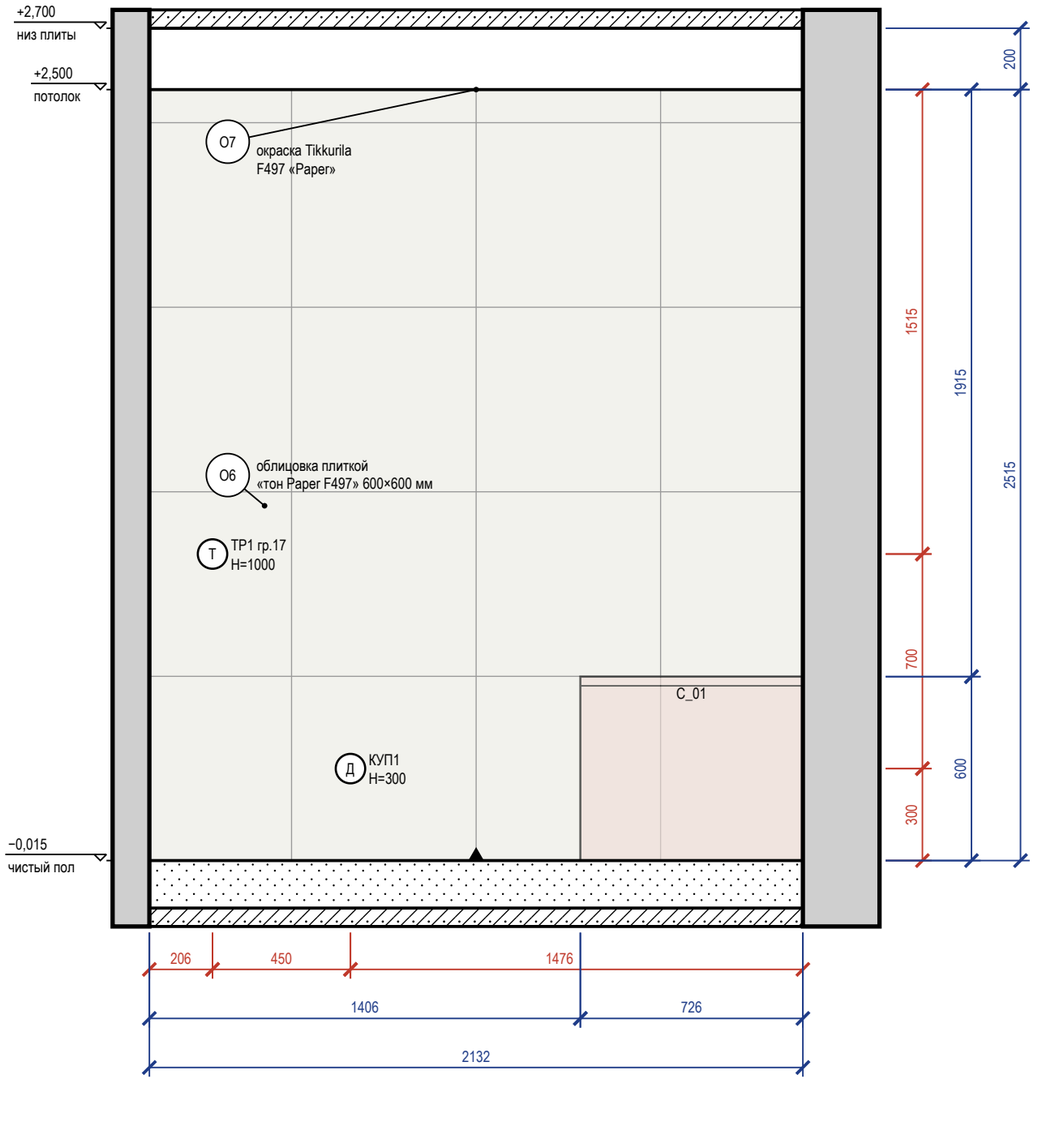


### Схема развёрток (М 1:100)

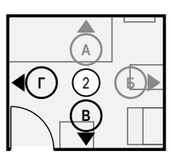


### Ведомость отделки (на листе)

| Марка | Поверхность | Материал, изделие | Цвет, код | Кол. |
|---|---|---|---|---|
| О6 | стены | облицовка плиткой, 600×600×9 мм, аналог: керамогранит матовый, тон F497, затирка CG2WA | #F1F1EC «тон Paper F497» | 10,2 м² |
| О7 | потолок | окраска, Tikkurila Luja 7, матовая, подготовка Q3 | Tikkurila F497 «Paper» | 5,6 м² |

### Примечания

1. Размеры — в мм от чистовых поверхностей стен; условные обозначения и общие указания — лист 2.
2. Схема мебели, приборов и декора не является технической документацией для производства мебели; габариты — по паспортам изделий.
3. Облицовка — по сетке швов 2 мм, раскладка от оси стены (треугольник у пола); подрезки — по листу раскладки плитки.
4. Гидроизоляция в 2 слоя, заход на стены 200 мм, в зоне душа — 2100 мм — до облицовки, с актом скрытых работ и тестом проливом (узел — на листе узлов).
5. Картины и зеркала крепить к основанию по паспорту изделия (закладные и анкеры — в перечне скрытых работ); крест — ось центра предмета.

| | | | | | |
|---|---|---|---|---|---|
| | | | | | Проект: Четырёхкомнатная квартира |
| | Лист | № док. | Подпись | Дата | Развёртки стен В, Г. Ванная комната (пом. 2) |
| Дизайнер | Кырлан А.С. | | | 05.10.26 | |

| Стадия | Лист | Листов |
|---|---|---|
| П | 47 | 111 |


выпуск 05.10.2026 № 05166c8858 · стр. 47 из 111




| | | | | | |
|---|---|---|---|---|---|
| | | | | | Проект: Четырёхкомнатная квартира |
| | Лист | № док. | Подпись | Дата | |
| Дизайнер | Кырлан А.С. | | | 05.10.26 | Визуализация: Тёмная комната |
| | | | | | Стадия: П; Лист: 48; Листов: 111 |

выпуск 05.10.2026 № 05166c8858 · стр. 48 из 111

## Развёртка стены А

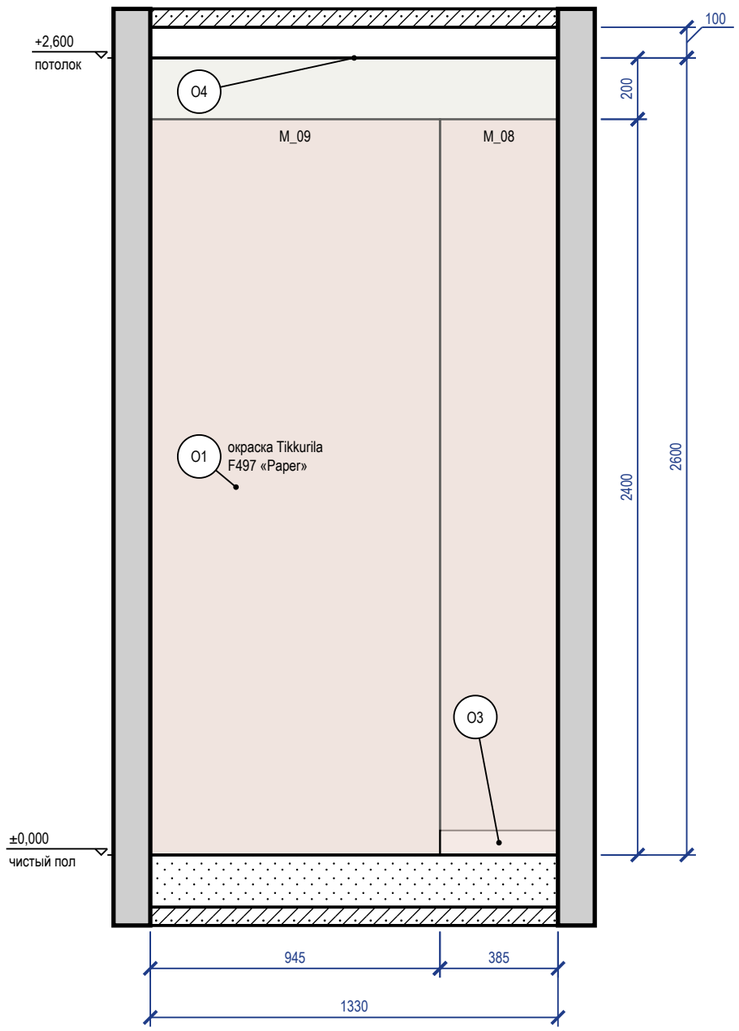



## Развёртка стены Б

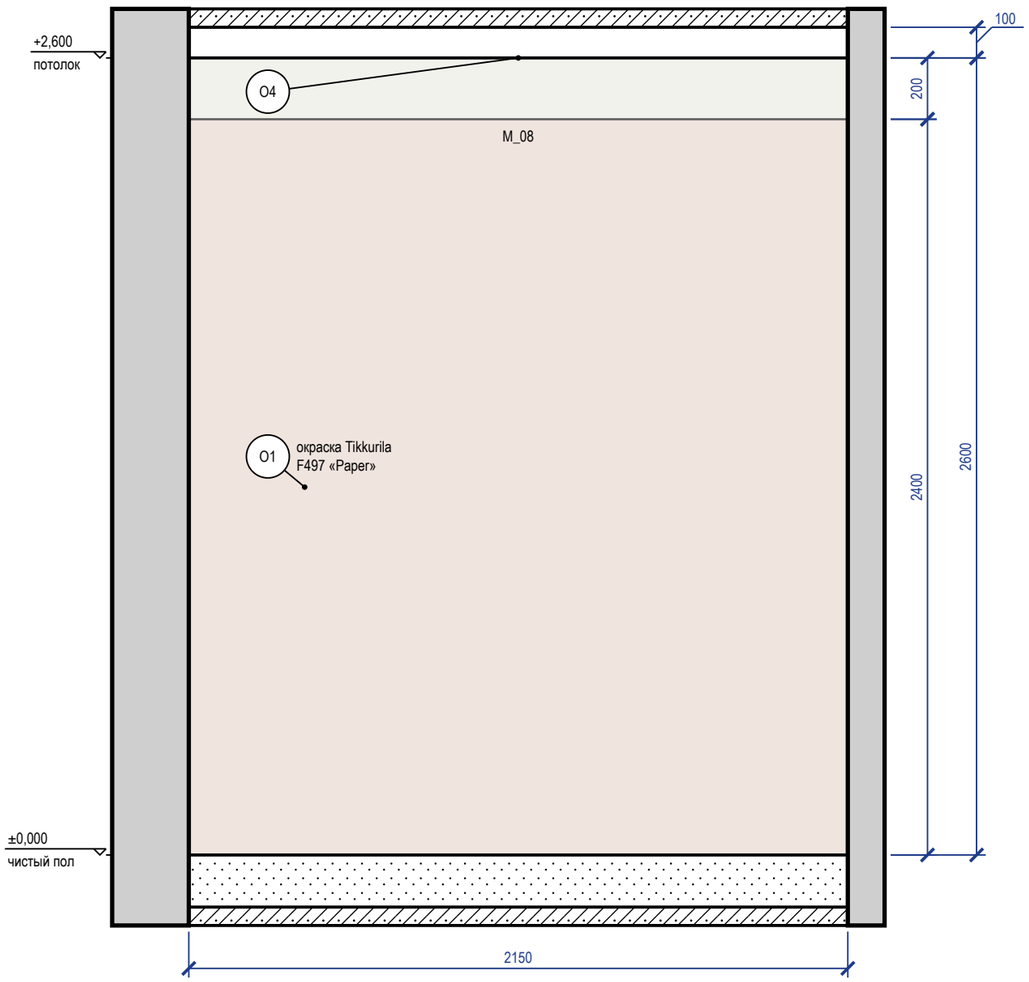


Визуализация этой стены — лист 48



### Схема развёрток (М 1:100)

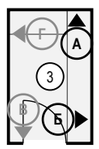


### Ведомость отделки (на листе)

| Марка | Поверхность | Материал, изделие | Цвет, код | Кол. |
|---|---|---|---|---|
| О1 | стены | окраска, Tikkurila Optiva 5 Matt, матовая, подготовка К3 | Tikkurila F497 «Paper» | 9 м² |
| О3 | плинтус | плинтус МДФ, h 80 мм, аналог: плинтус МДФ под окраску 80×16 мм, полуглянцевая | Tikkurila F497 «Paper» | 0,4 м |
| О4 | потолок | окраска, Tikkurila Anti-Reflex 2, глубокоматовая, подготовка Q3 | Tikkurila F497 «Paper» | 3 м² |

### Примечания


1. Размеры — в мм от чистовых поверхностей стен; условные обозначения и общие указания — лист 2.

| | | | | | |
|---|---|---|---|---|---|
| | | | | | Проект: Четырёхкомнатная квартира |
| | Лист | № док. | Подпись | Дата | |
| Дизайнер | Кырлан А.С. | | | 05.10.26 | Развёртки стен А, Б. Тёмная комната (пом. 3) |


| Стадия | Лист | Листов |
|---|---|---|
| П | 49 | 111 |

выпуск 05.10.2026 № 05166c8858 · стр. 49 из 111


## Развёртка стены В

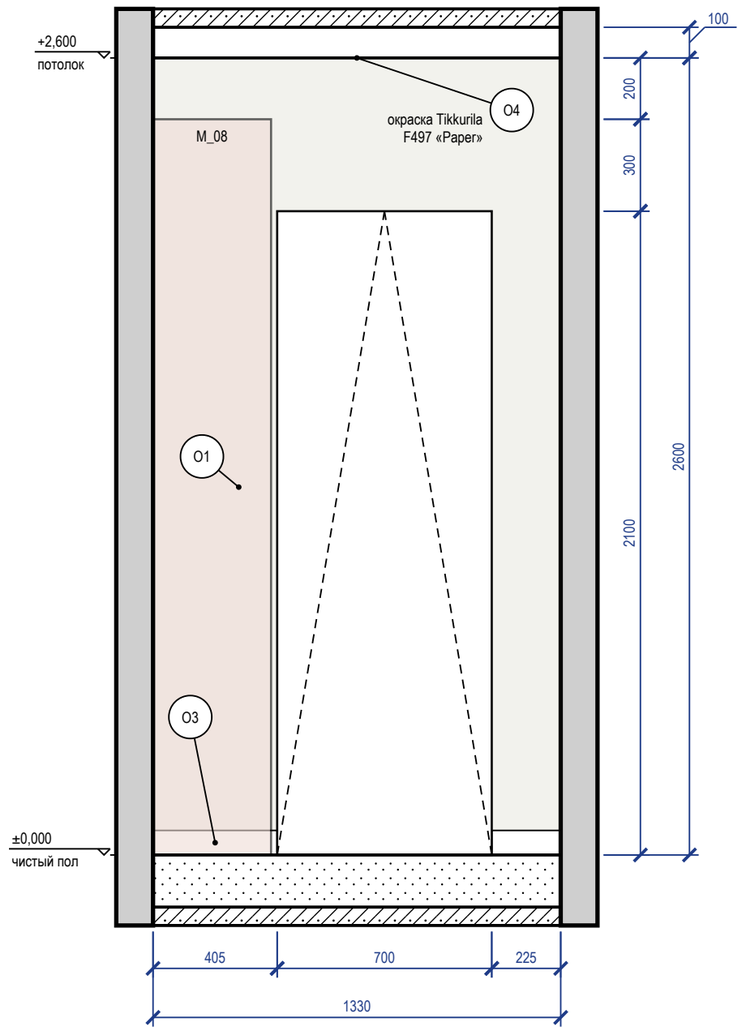


## Развёртка стены Г

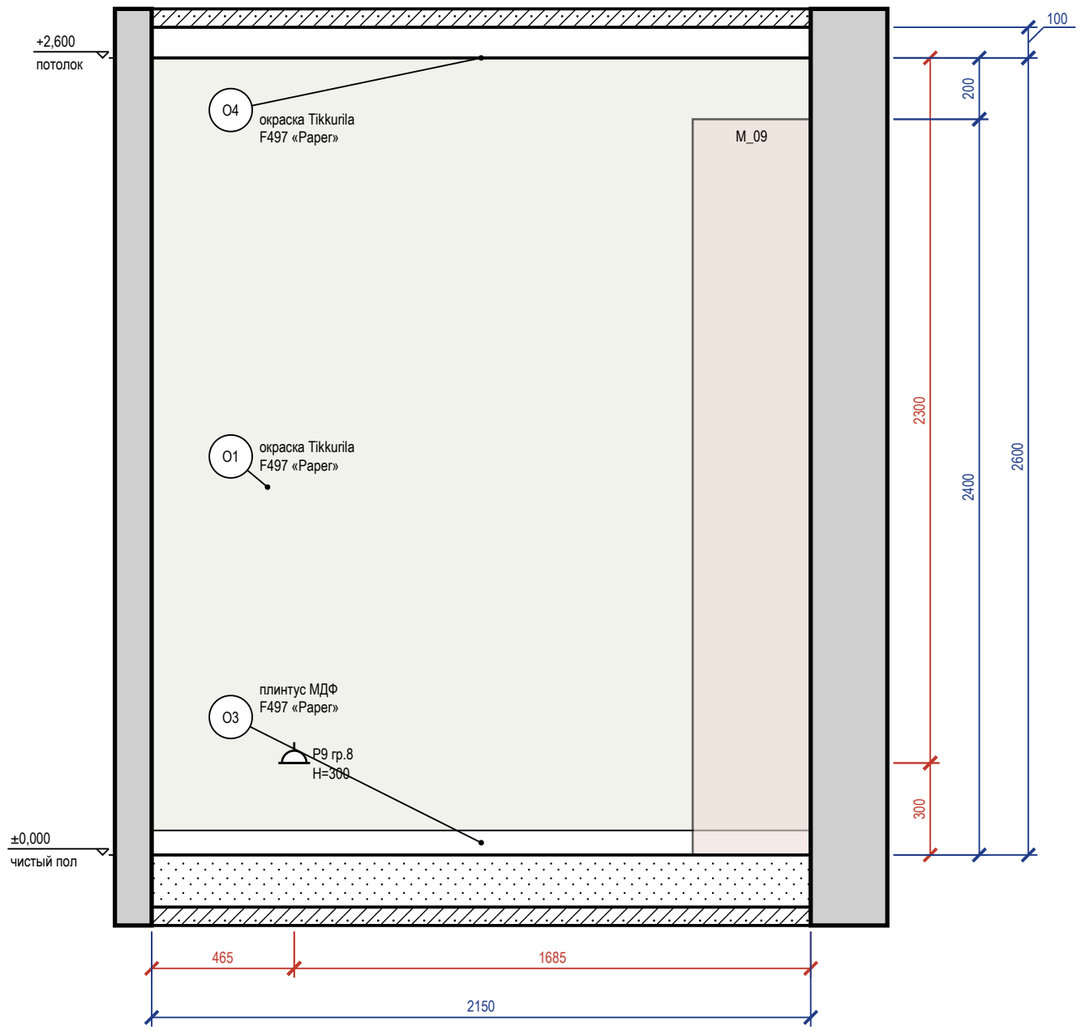


### Схема развёрток (М 1:100)

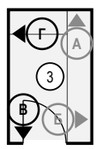


### Ведомость отделки (на листе)

| Марка | Поверхность | Материал, изделие | Цвет, код | Кол. |
|---|---|---|---|---|
| О1 | стены | окраска, Tikkurila Optiva 5 Matt, матовая, подготовка К3 | Tikkurila F497 «Paper» | 7,6 м² |
| О3 | плинтус | плинтус МДФ, h 80 мм, аналог: плинтус МДФ под окраску 80×16 мм, полуглянцевая | Tikkurila F497 «Paper» | 2,8 м |
| О4 | потолок | окраска, Tikkurila Anti-Reflex 2, глубокоматовая, подготовка Q3 | Tikkurila F497 «Paper» | 3 м² |

### Примечания

1. Размеры — в мм от чистовых поверхностей стен; условные обозначения и общие указания — лист 2.

| | | | | | |
|---|---|---|---|---|---|
| | | | | | Проект: Четырёхкомнатная квартира |
| | Лист | № док. | Подпись | Дата | |
| Дизайнер | Кырлан А.С. | | | 05.10.26 | Развёртки стен В, Г. Тёмная комната (пом. 3) |

| Стадия | Лист | Листов |
|---|---|---|
| П | 50 | 111 |

выпуск 05.10.2026 № 05166c8858 · стр. 50 из 111



| | | | | | |
|---|---|---|---|---|---|
| | | | | | Проект: Четырёхкомнатная квартира |
| | Лист | № док. | Подпись | Дата | |
| Дизайнер | Кырлан А.С. | | | 05.10.26 | Визуализация: Детская 1 |

| Стадия | Лист | Листов |
|---|---|---|
| П | 51 | 111 |

выпуск 05.10.2026 № 05166c8858 · стр. 51 из 111




| | | | | | |
|---|---|---|---|---|---|
| | | | | | Проект: Четырёхкомнатная квартира |
| | Лист | № док. | Подпись | Дата | |
| Дизайнер | Кырлан А.С. | | | 05.10.26 | Визуализация: Детская 1 |


| Стадия | Лист | Листов |
|---|---|---|
| П | 52 | 111 |

выпуск 05.10.2026 № 0516c8858 · стр. 52 из 111

## Развёртка стены А

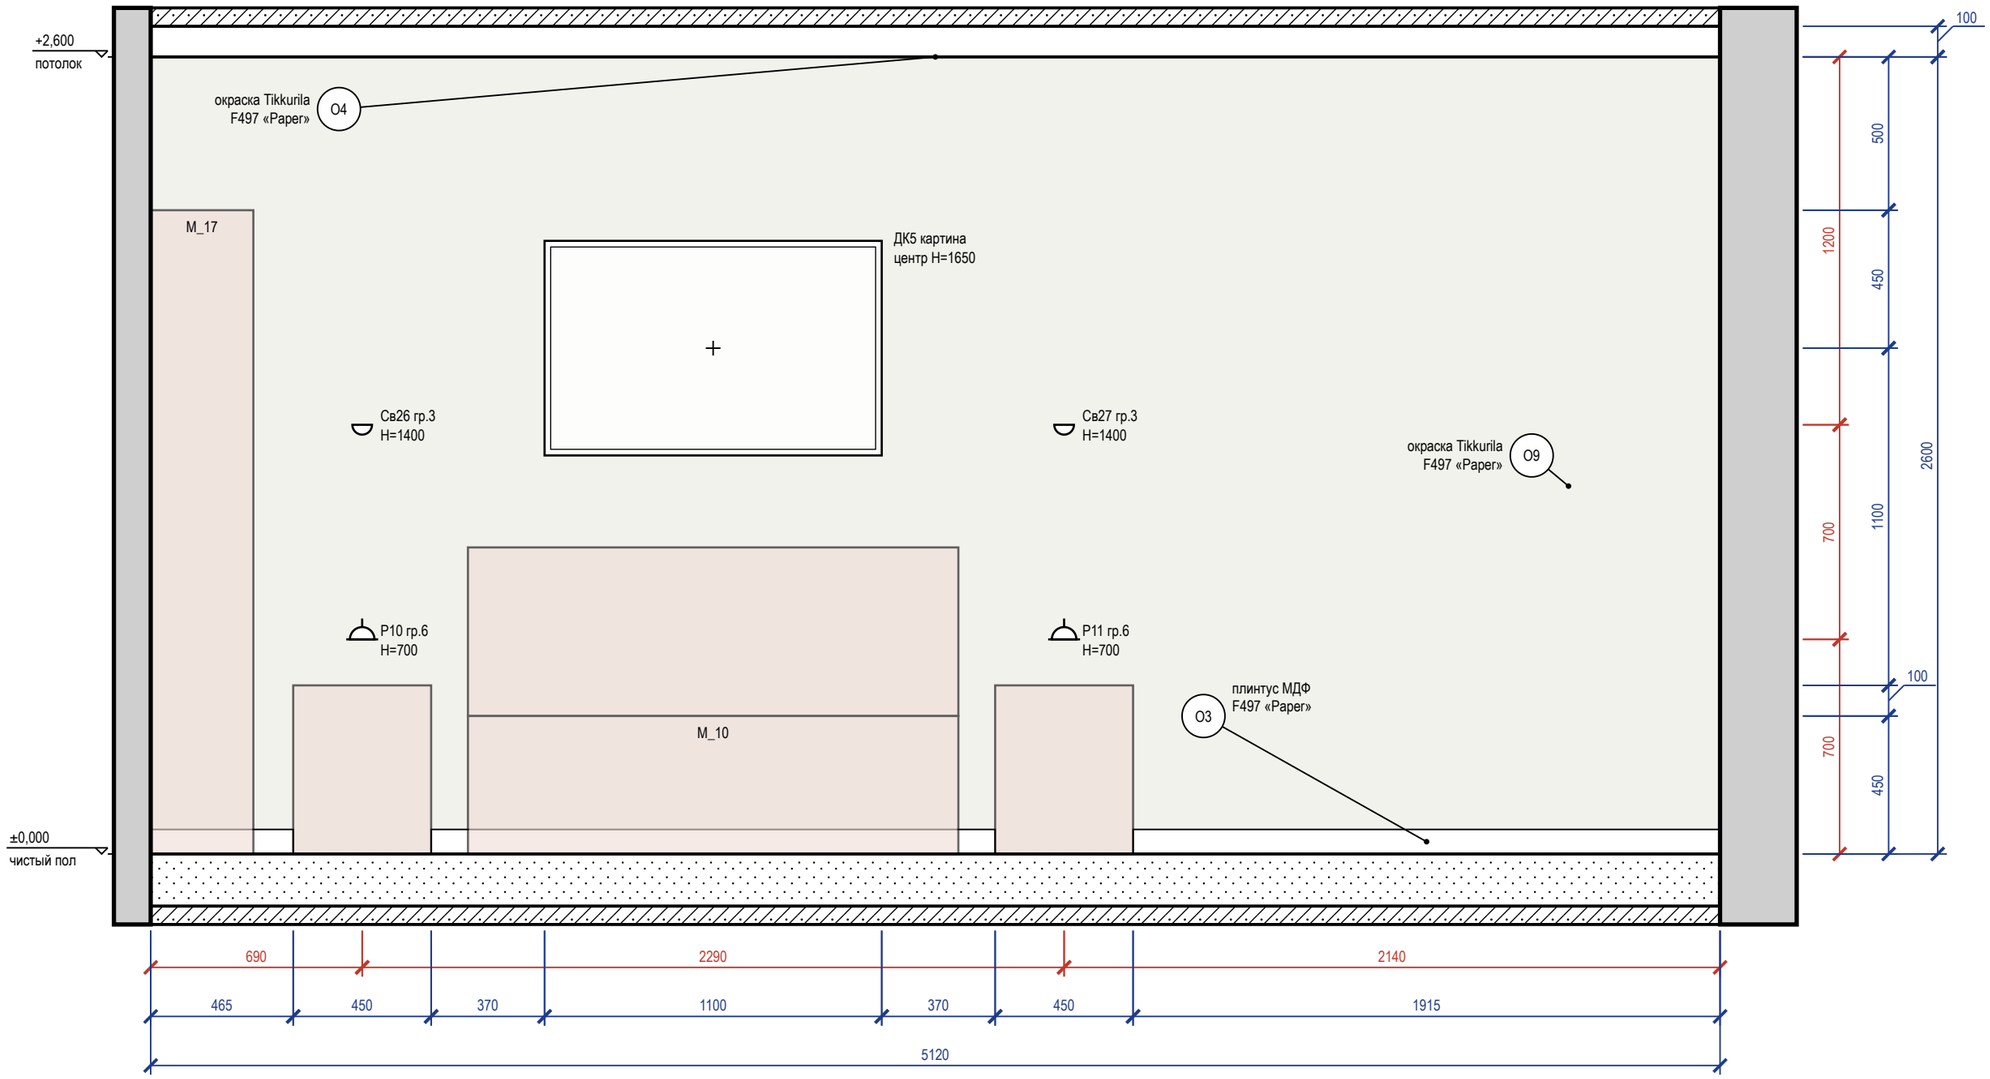


### Схема развёрток (М 1:100)

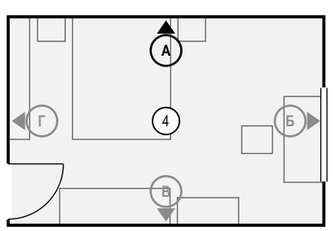


### Ведомость отделки (на листе)

| Марка | Поверхность | Материал, изделие | Цвет, код | Кол. |
|---|---|---|---|---|
| О3 | плинтус | плинтус МДФ, h 80 мм, аналог: плинтус МДФ под окраску 80×16 мм, полуглянцевая | Tikkurila F497 «Paper» | 4,2 м |
| О4 | потолок | окраска, Tikkurila Anti-Reflex 2, глубокоматовая, подготовка Q3 | Tikkurila F497 «Paper» | 17,5 м² |
| О9 | стены | окраска, Tikkurila Joker, шелковисто-матовая, подготовка К3 | Tikkurila F497 «Paper» | 13,3 м² |

### Примечания

1. Размеры — в мм от чистовых поверхностей стен; условные обозначения и общие указания — лист 2.
2. Картины и зеркала крепить к основанию по паспорту изделия (закладные и анкеры — в перечне скрытых работ); крест — ось центра предмета.

| | | | | |
|---|---|---|---|---|
| | Лист | № док. | Подпись | Дата |
| Дизайнер | Кырлан А.С. | | | 05.10.26 |


Проект: Четырёхкомнатная квартира

Развёртка стены А. Детская 1 (пом. 4)


| Стадия | Лист | Листов |
|---|---|---|
| П | 53 | 111 |

выпуск 05.10.2026 № 05166c8858 · стр. 53 из 111

## Развёртка стены Б

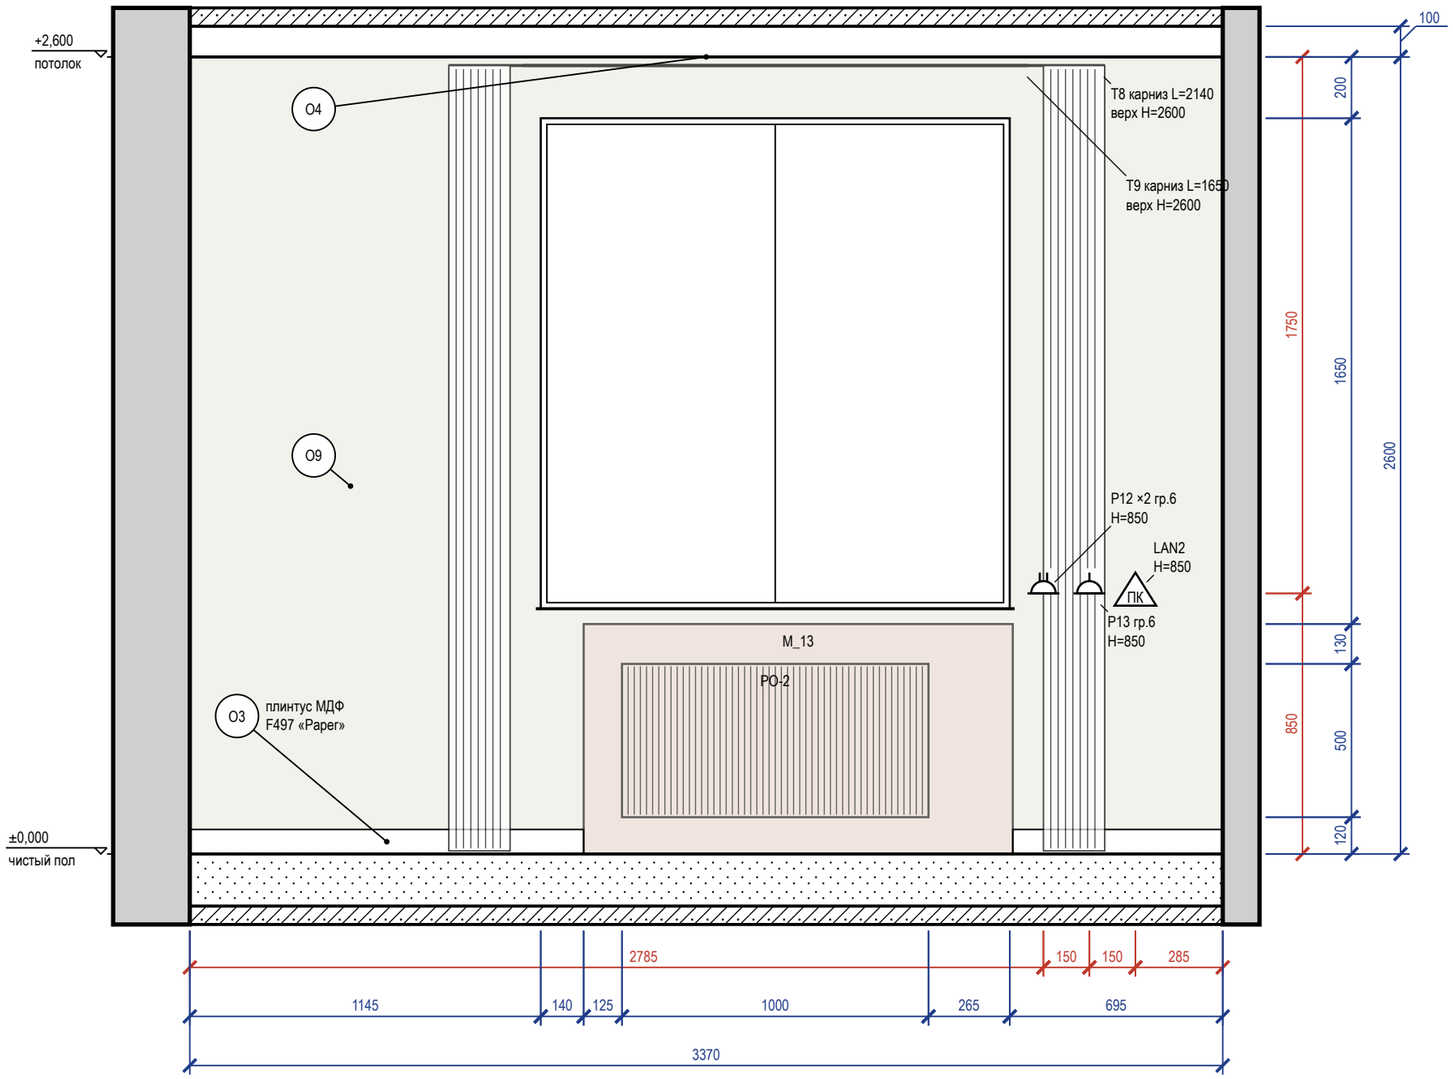


### Схема развёрток (М 1:100)

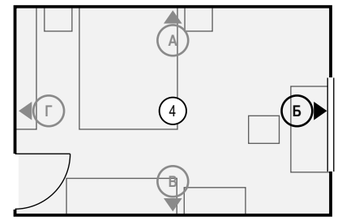


### Ведомость отделки (на листе)

| Марка | Поверхность | Материал, изделие | Цвет, код | Кол. |
|---|---|---|---|---|
| О3 | плинтус | плинтус МДФ, h 80 мм, аналог: плинтус МДФ под окраску 80×16 мм, полуглянцевая | Tikkurila F497 «Paperi» | 2 м |
| О4 | потолок | окраска, Tikkurila Anti-Reflex 2, глубокоматовая, подготовка Q3 | Tikkurila F497 «Paperi» | 17,5 м² |
| О9 | стены | окраска, Tikkurila Joker, шелковисто-матовая, подготовка К3 | Tikkurila F497 «Paperi» | 6,3 м² |

### Примечания

1. Размеры — в мм от чистовых поверхностей стен; условные обозначения и общие указания — лист 2.
2. Карнизы (шины) — по ведомости текстиля декоратора; длина L и верх H — по развёртке, крепление — до окраски потолка.
3. Линии узора (швы плитки, складки штор, рёбра радиаторов) прерываются у знаков и выносок — просвет между линиями не менее 0,7 мм.

| | Лист | № док. | Подпись | Дата |
|---|---|---|---|---|
| Дизайнер | Кырлан А.С. | | | 05.10.26 |


Проект: Четырёхкомнатная квартира

Развёртка стены Б. Детская 1 (пом. 4)


| Стадия | Лист | Листов |
|---|---|---|
| П | 54 | 111 |

выпуск 05.10.2026 № 05166c8858 · стр. 54 из 111

## Развёртка стены В

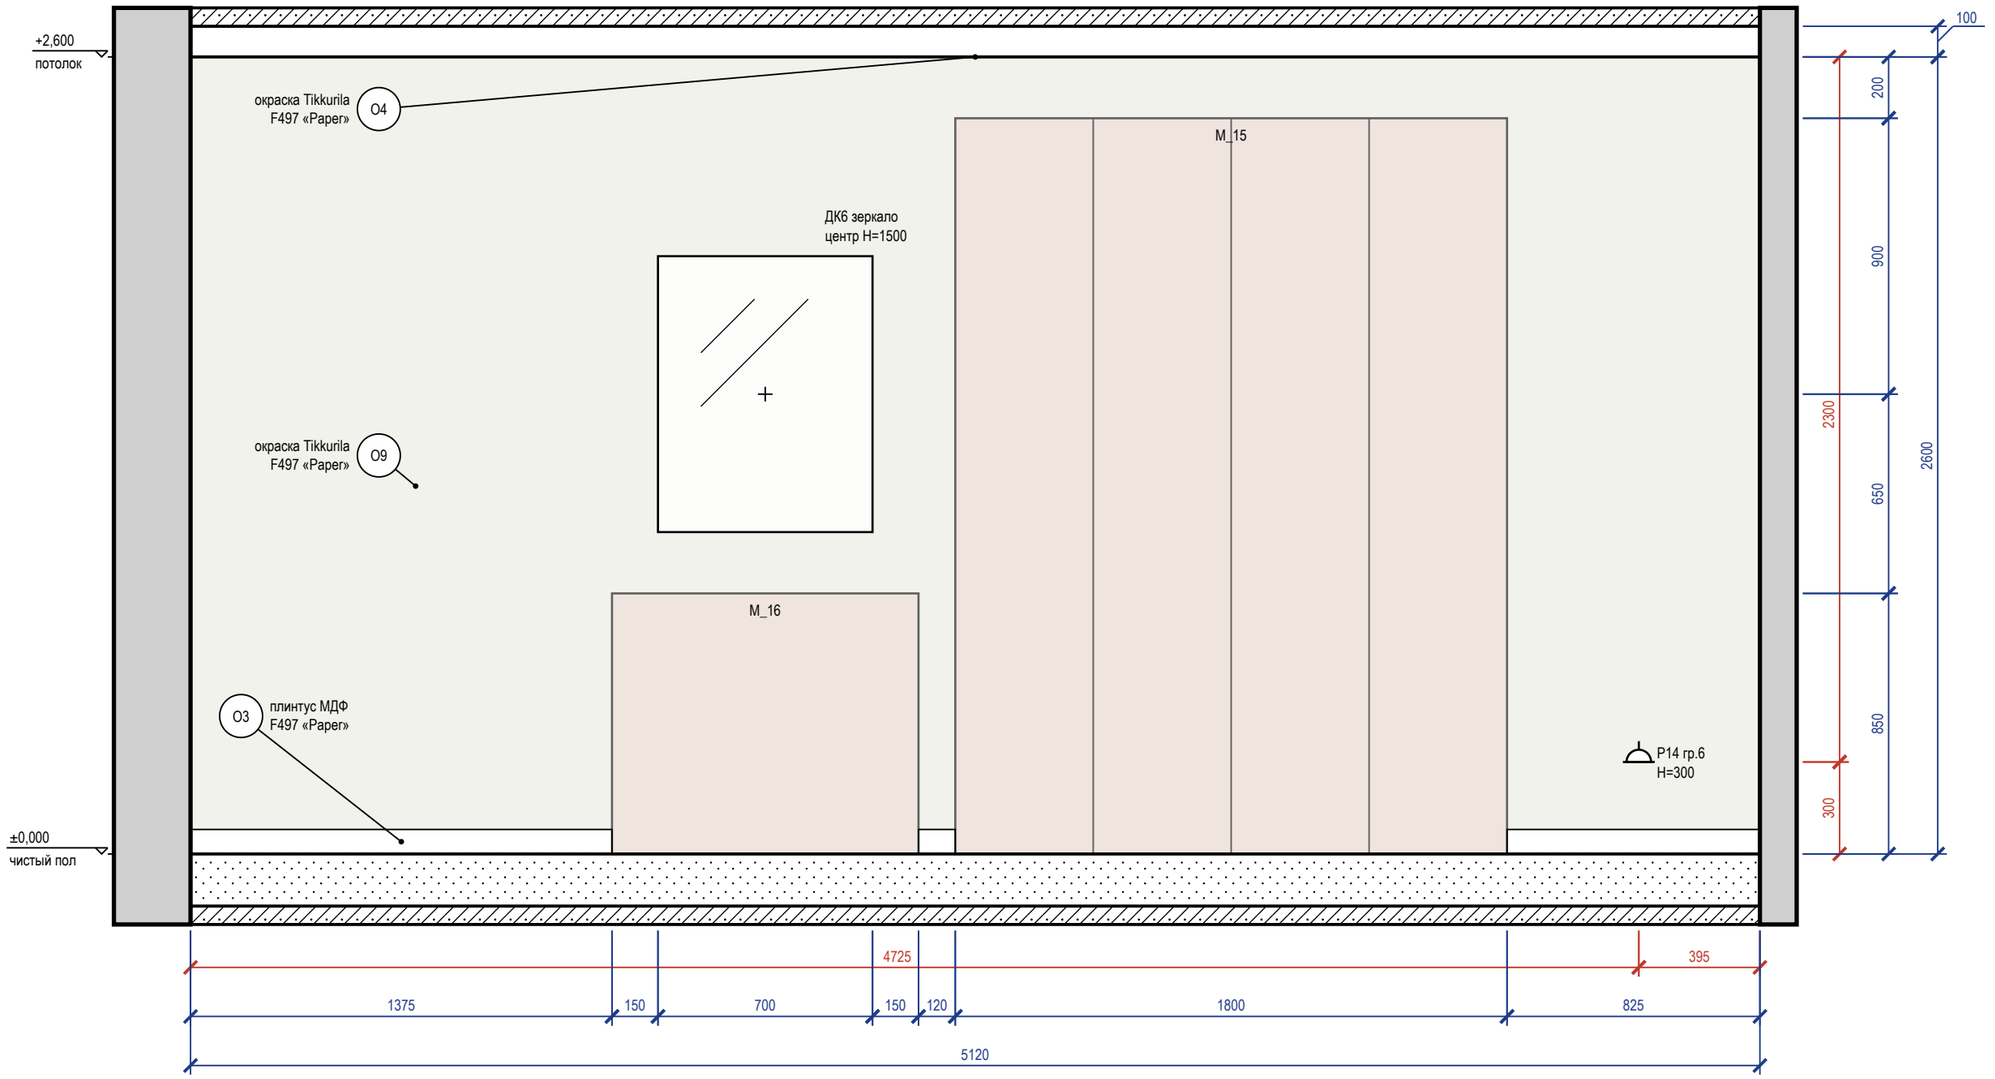



### Схема развёрток (М 1:100)

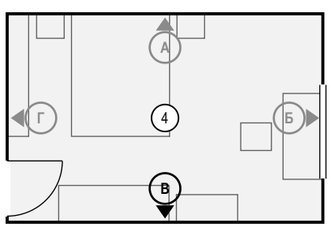


### Ведомость отделки (на листе)

| Марка | Поверхность | Материал, изделие | Цвет, код | Кол. |
|---|---|---|---|---|
| O3 | плинтус | плинтус МДФ, h 80 мм, аналог: плинтус МДФ под окраску 80×16 мм, полуглянцевая | Tikkurila F497 «Paper» | 2,3 м |
| O4 | потолок | окраска, Tikkurila Anti-Reflex 2, глубокоматовая, подготовка Q3 | Tikkurila F497 «Paper» | 17,5 м² |
| O9 | стены | окраска, Tikkurila Joker, шелковисто-матовая, подготовка K3 | Tikkurila F497 «Paper» | 13,3 м² |

Визуализация этой стены — лист 51

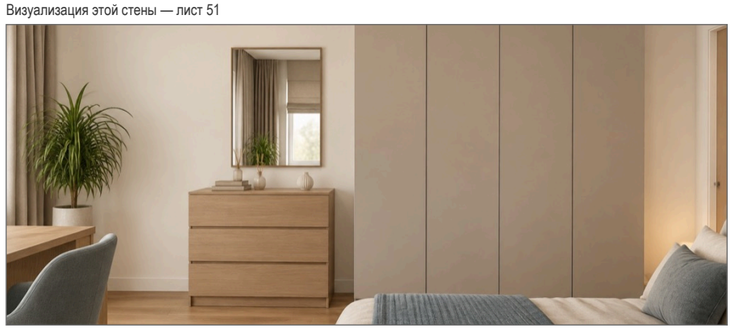

### Примечания


1. Размеры — в мм от чистовых поверхностей стен; условные обозначения и общие указания — лист 2.
2. Картины и зеркала крепить к основанию по паспорту изделия (закладные и анкеры — в перечне скрытых работ); крест — ось центра предмета.

| | | | | | |
|---|---|---|---|---|---|
| | | | | | Проект: Четырёхкомнатная квартира |
| | Лист | № док. | Подпись | Дата | |
| Дизайнер | Кырлан А.С. | | | 05.10.26 | Развёртка стены В. Детская 1 (пом. 4) |


| Стадия | Лист | Листов |
|---|---|---|
| П | 55 | 111 |

выпуск 05.10.2026 № 05166c8858 · стр. 55 из 111

## Развёртка стены Г

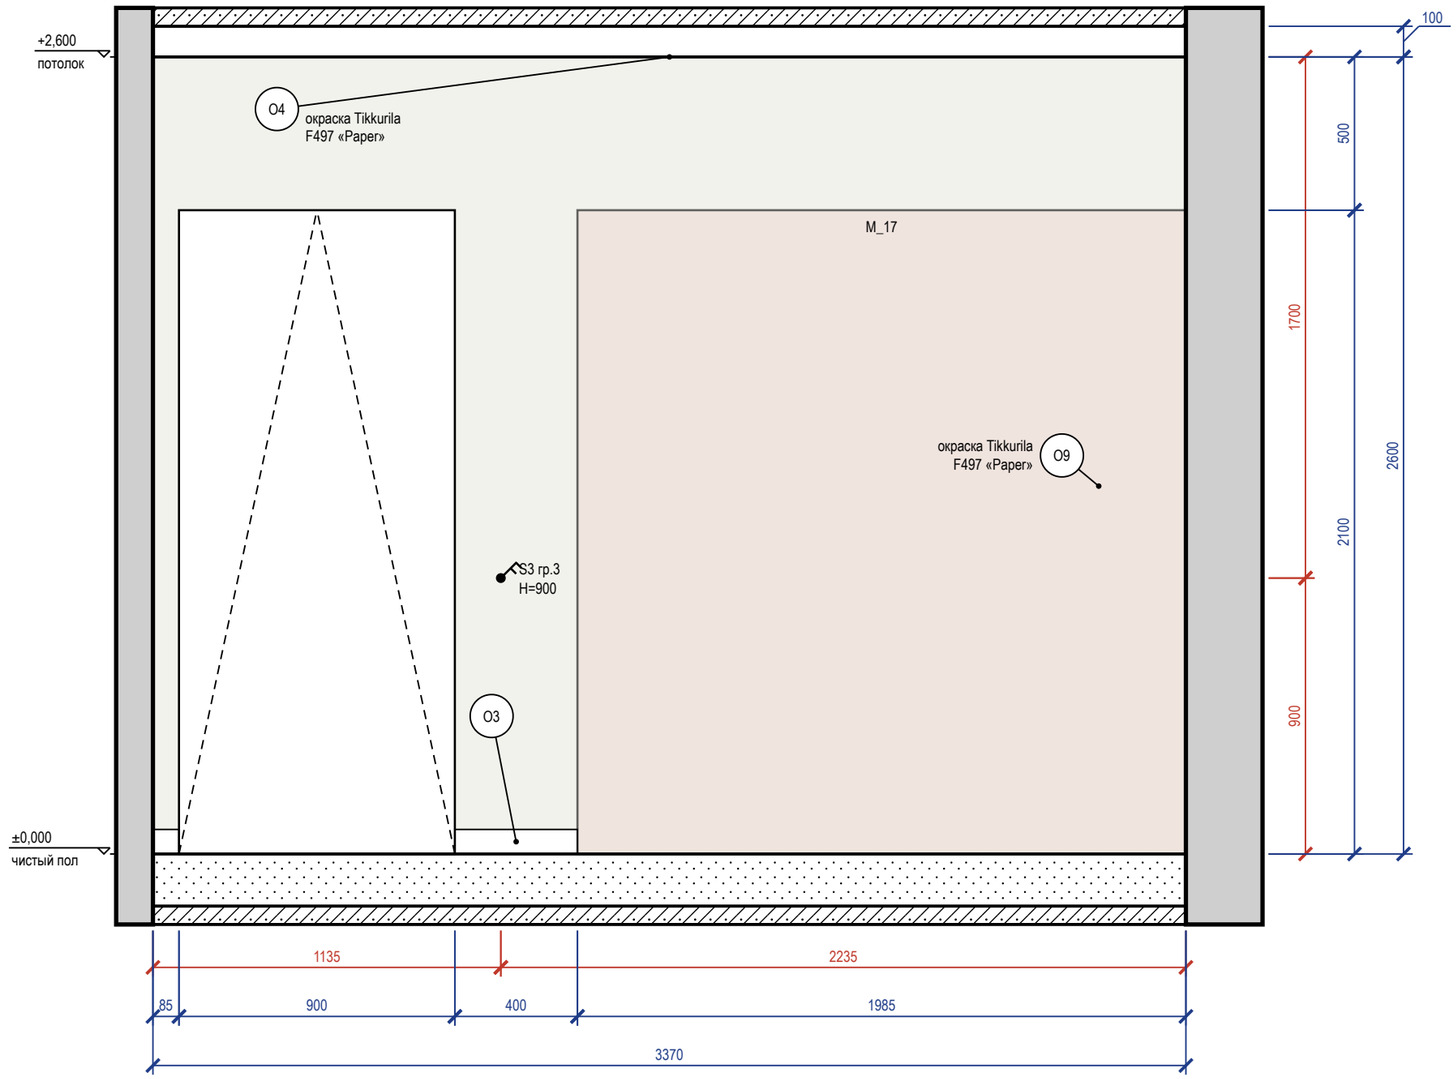


## Схема развёрток (М 1:100)

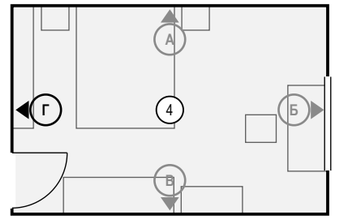


## Ведомость отделки (на листе)

| Марка | Поверхность | Материал, изделие | Цвет, код | Кол. |
|---|---|---|---|---|
| О3 | плинтус | плинтус МДФ, h 80 мм, аналог: плинтус МДФ под окраску 80×16 мм, полуглянцевая | Tikkurila F497 «Paper» | 0,5 м |
| О4 | потолок | окраска, Tikkurila Anti-Reflex 2, глубокоматовая, подготовка Q3 | Tikkurila F497 «Paper» | 17,5 м² |
| О9 | стены | окраска, Tikkurila Joker, шелковисто-матовая, подготовка К3 | Tikkurila F497 «Paper» | 6,9 м² |

Визуализация этой стены — лист 52



### Примечания

1. Размеры — в мм от чистовых поверхностей стен; условные обозначения и общие указания — лист 2.

| | | | | | |
|---|---|---|---|---|---|
| | | | | | Проект: Четырёхкомнатная квартира |
| | Лист | № док. | Подпись | Дата | Развёртка стены Г. Детская 1 (пом. 4) |
| Дизайнер | Кырлан А.С. | | | 05.10.26 | |

| Стадия | Лист | Листов |
|---|---|---|
| П | 56 | 111 |

выпуск 05.10.2026 № 05166c8858 · стр. 56 из 111



| | | | | | |
|---|---|---|---|---|---|
| | | | | | Проект: Четырёхкомнатная квартира |
| | Лист | № док. | Подпись | Дата | Визуализация коридора |
| Дизайнер | Кырлан А.С. | | | 05.10.26 | |

| Стадия | Лист | Листов |
|---|---|---|
| П | 57 | 111 |


выпуск 05.10.2026 № 0516c8858 · стр. 57 из 111




| | | | | | | |
|---|---|---|---|---|---|---|
| | | | | | Проект: Четырёхкомнатная квартира | |
| | | | | | | |
| | Лист | № док. | Подпись | Дата | | |
| Дизайнер | Кырлан А.С. | | | 05.10.26 | Визуализация коридора | Стадия / Лист / Листов |
| | | | | | | П / 58 / 111 |

выпуск 05.10.2026 № 05166c8858 · стр. 58 из 111


## Развёртка стены А

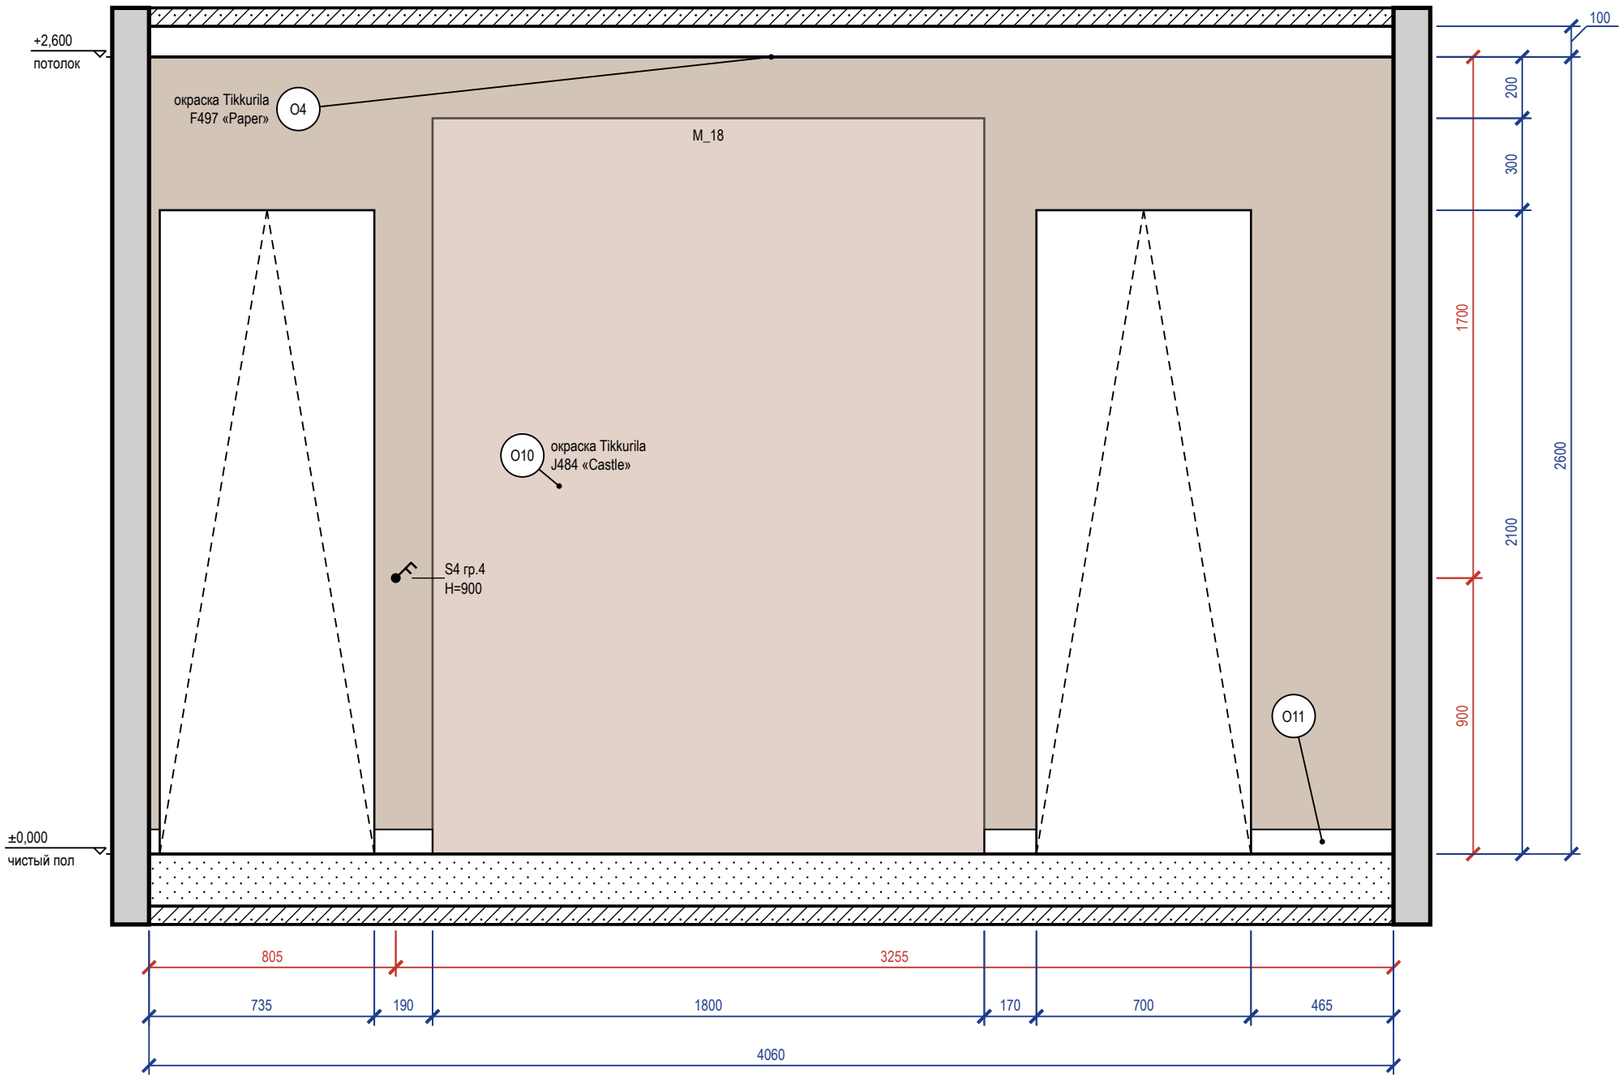


## Развёртка стены Б

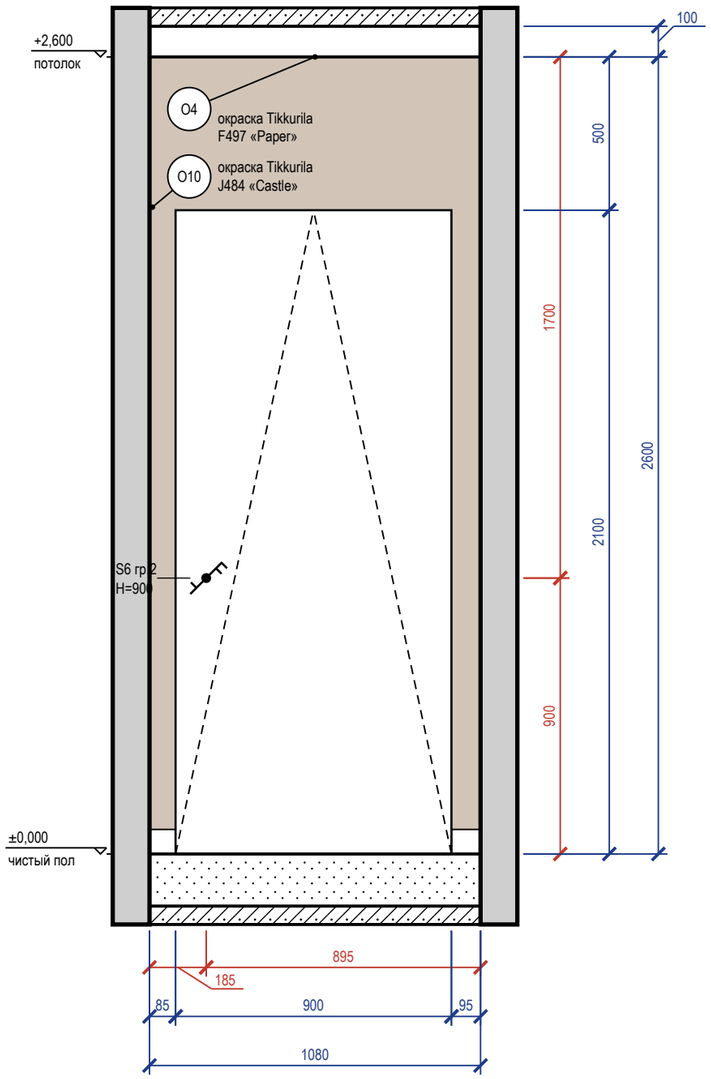


### Схема развёрток (М 1:100)

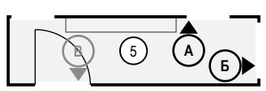


### Ведомость отделки (на листе)

| Марка | Поверхность | Материал, изделие | Цвет, код | Кол. |
|---|---|---|---|---|
| O4 | потолок | окраска, Tikkurila Anti-Reflex 2, глубокоматовая, подготовка Q3 | Tikkurila F497 «Paper» | 4,5 м² |
| O10 | стены | окраска, Tikkurila Optiva 20 Semimatt, шелковисто-матовая, подготовка K3 | Tikkurila J484 «Castle» | 8,5 м² |
| O11 | плинтус | плинтус МДФ, h 80 мм, аналог: плинтус МДФ под окраску 80×16 мм, полуглянцевая | Tikkurila J484 «Castle» | 1 м |

Визуализация этой стены — лист 57




### Примечания

1. Размеры — в мм от чистовых поверхностей стен; условные обозначения и общие указания — лист 2.


| | | | | | |
|---|---|---|---|---|---|
| | | | | | Проект: Четырёхкомнатная квартира |
| | Лист | № док. | Подпись | Дата | |
| Дизайнер | Кырлан А.С. | | | 05.10.26 | Развёртки стен А, Б. Коридор (пом. 5) |
| | | | | | Стадия: П; Лист: 59; Листов: 111 |

выпуск 05.10.2026 № 05166c8858 · стр. 59 из 111

## Развёртка стены В

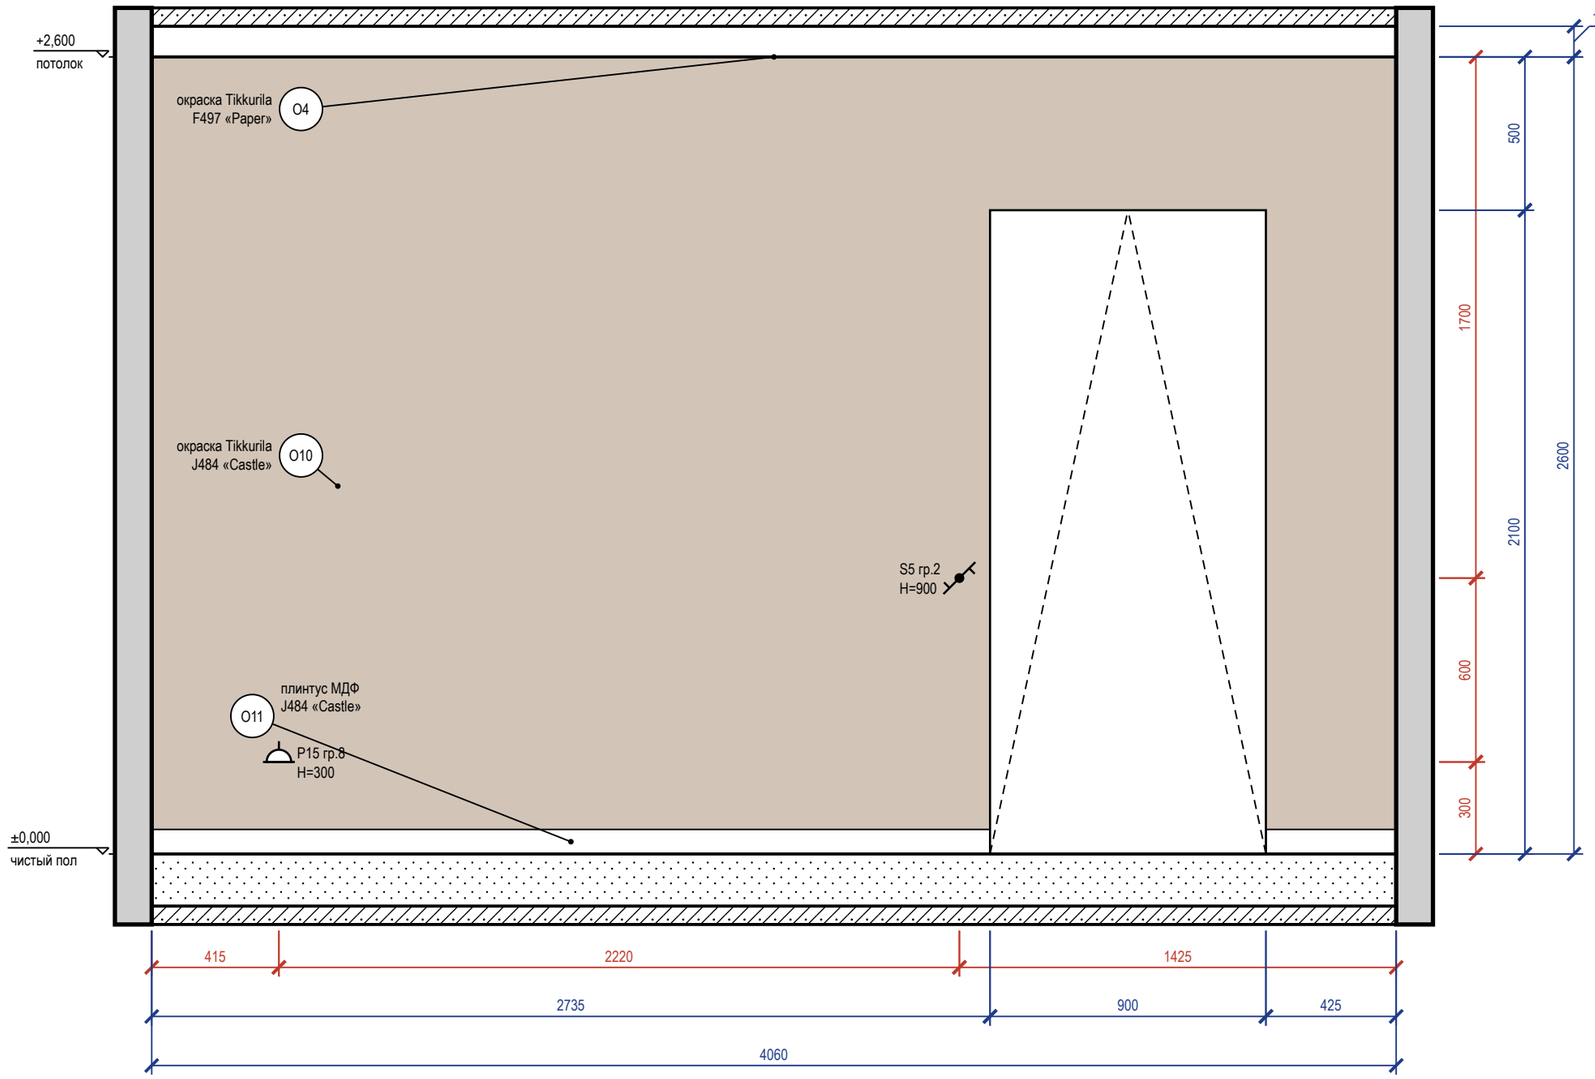



## Схема развёрток (М 1:100)

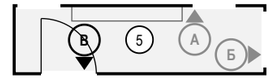


## Ведомость отделки (на листе)

| Марка | Поверхность | Материал, изделие | Цвет, код | Кол. |
|---|---|---|---|---|
| О4 | потолок | окраска, Tikkurila Anti-Reflex 2, глубокоматовая, подготовка Q3 | Tikkurila F497 «Paper» | 4,5 м² |
| О10 | стены | окраска, Tikkurila Optiva 20 Semimatt, шелковисто-матовая, подготовка К3 | Tikkurila J484 «Castle» | 8,7 м² |
| О11 | плинтус | плинтус МДФ, h 80 мм, аналог: плинтус МДФ под окраску 80×16 мм, полуглянцевая | Tikkurila J484 «Castle» | 3,2 м |

Визуализация этой стены — лист 58

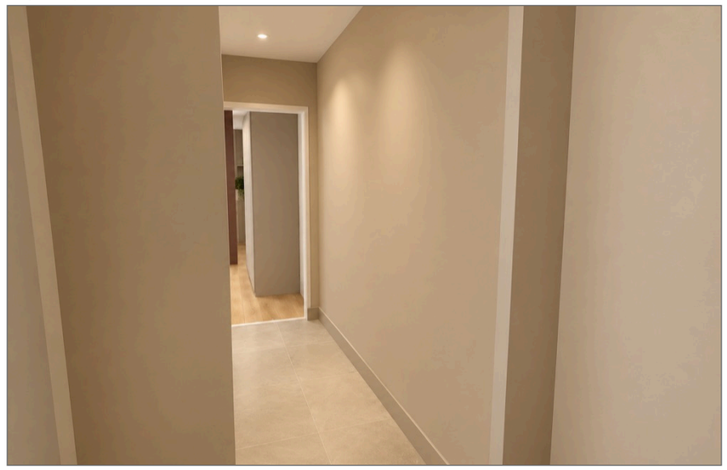

### Примечания

1. Размеры — в мм от чистовых поверхностей стен; условные обозначения и общие указания — лист 2.

| | | | | | |
|---|---|---|---|---|---|
| | | | | | Проект: Четырёхкомнатная квартира |
| | Лист | № док. | Подпись | Дата | Развёртка стены В. Коридор (пом. 5) |
| Дизайнер | Кырлан А.С. | | | 05.10.26 | |

| Стадия | Лист | Листов |
|---|---|---|
| П | 60 | 111 |

выпуск 05.10.2026 № 0516c8858 · стр. 60 из 111




| | | | | | |
|---|---|---|---|---|---|
| | | | | | Проект: Четырёхкомнатная квартира |
| | Лист | № док. | Подпись | Дата | |
| Дизайнер | Кырлан А.С. | | | 05.10.26 | Визуализация кухни |


| Стадия | Лист | Листов |
|---|---|---|
| П | 61 | 111 |

выпуск 05.10.2026 № 0516c8858 · стр. 61 из 111

## Развёртка стены А

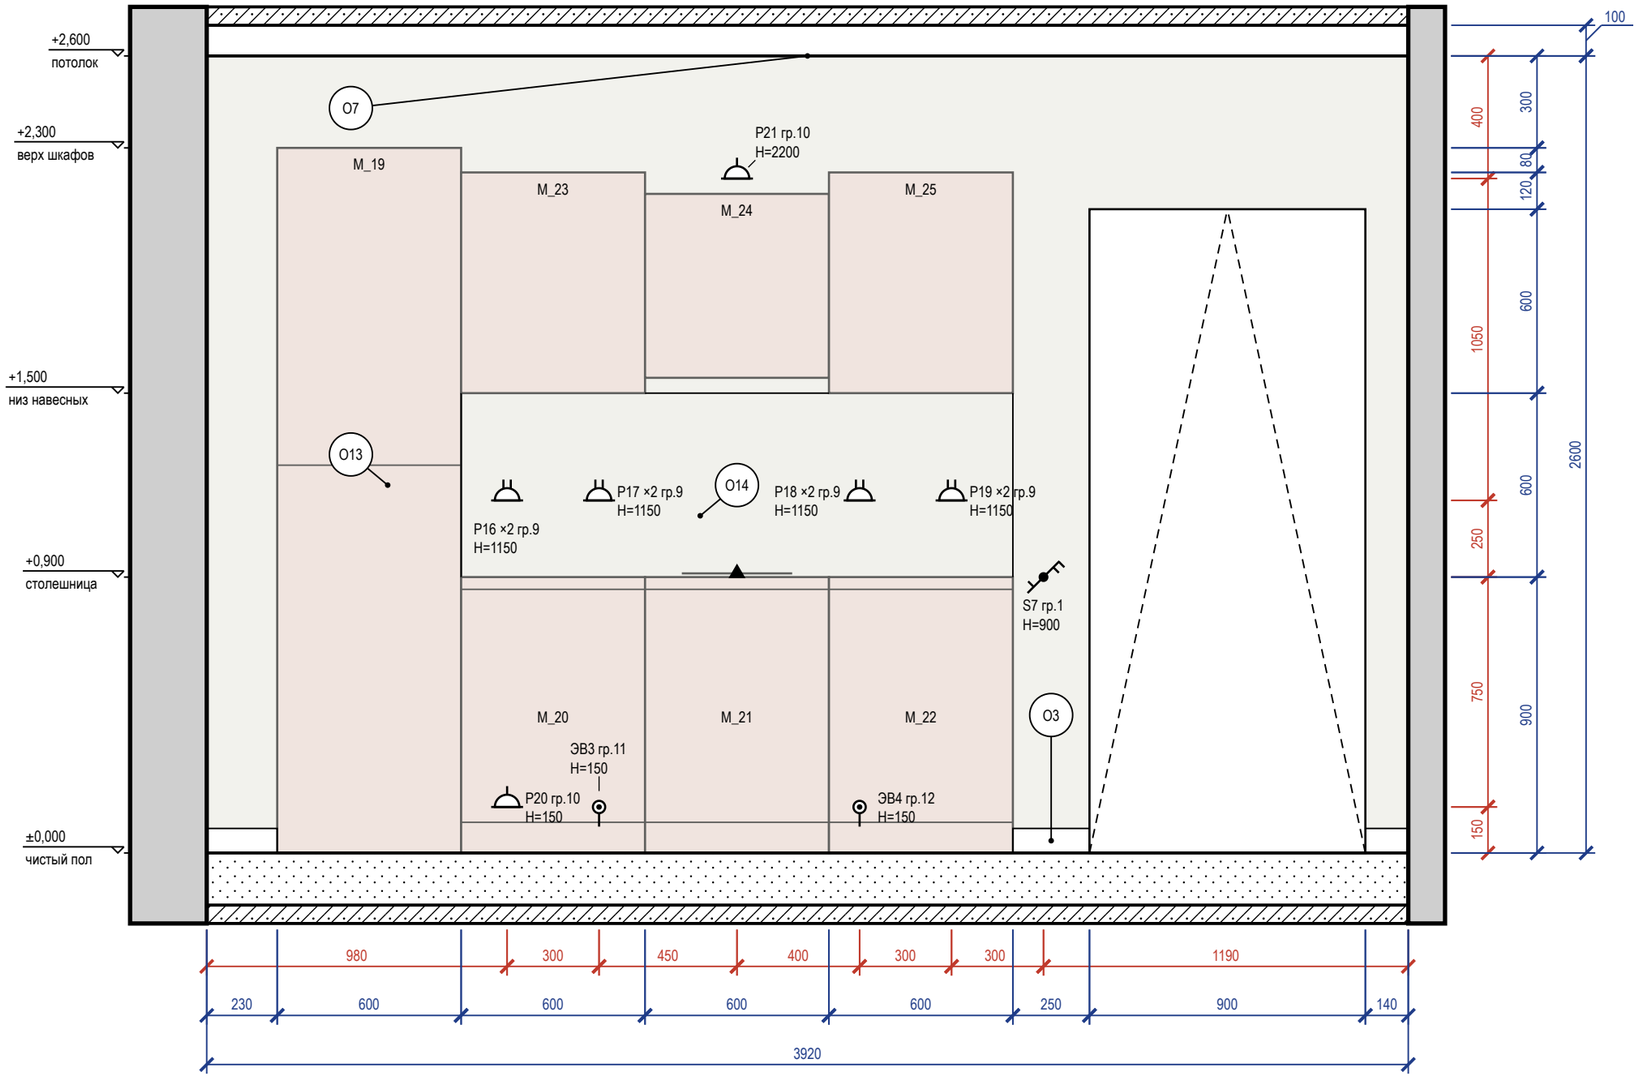


## Схема развёрток (М 1:100)

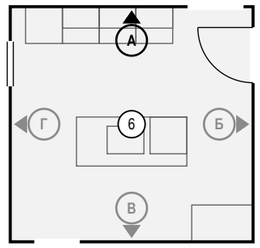


## Ведомость отделки (на листе)

| Марка | Поверхность | Материал, изделие | Цвет, код | Кол. |
|---|---|---|---|---|
| О3 | плинтус | плинтус МДФ, h 80 мм, аналог: плинтус МДФ под окраску 80×16 мм, полуглянцевая | Tikkurila F497 «Paper» | 0,6 м |
| О7 | потолок | окраска, Tikkurila Luja 7, матовая, подготовка Q3 | Tikkurila F497 «Paper» | 15,2 м² |
| О13 | стены | окраска, Tikkurila Luja 7, шелковисто-матовая, подготовка К3 | Tikkurila F497 «Paper» | 7,2 м² |
| О14 | фартук | керамогранит, 600×600×9 мм, аналог: керамогранит матовый, тон F497, затирка CG2WA | #F1F1EC «тон Paper F497» | 1,1 м² |

Визуализация этой стены — лист 61



### Примечания


1. Размеры — в мм от чистовых поверхностей стен; условные обозначения и общие указания — лист 2.

| | | | | | |
|---|---|---|---|---|---|
| | | | | | Проект: Четырёхкомнатная квартира |
| | Лист | № док. | Подпись | Дата | |
| Дизайнер | Кырлан А.С. | | | 05.10.26 | Развёртка стены А. Кухня (пом. 6), кухонный фронт |


| Стадия | Лист | Листов |
|---|---|---|
| П | 62 | 111 |

выпуск 05.10.2026 № 0516c8858 · стр. 62 из 111

## Развёртка стены Б

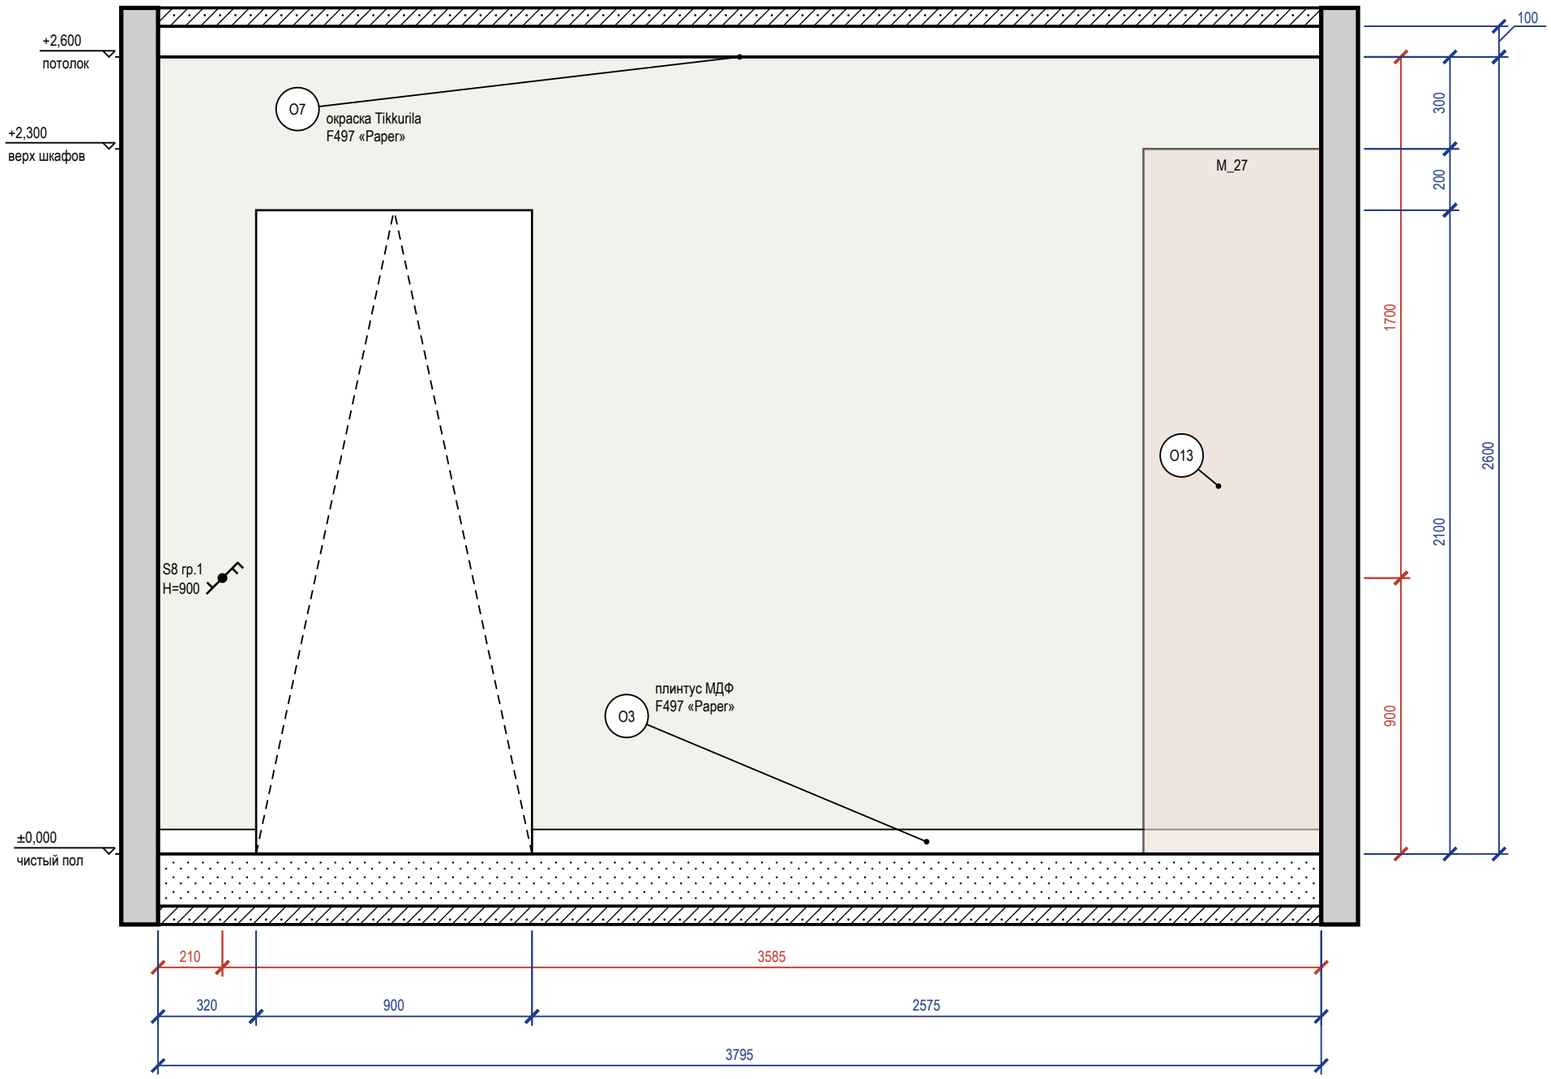


## Схема развёрток (М 1:100)

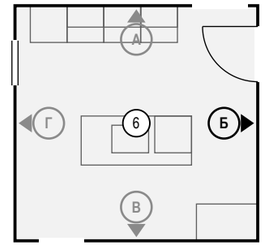


## Ведомость отделки (на листе)

| Марка | Поверхность | Материал, изделие | Цвет, код | Кол. |
|---|---|---|---|---|
| О3 | плинтус | плинтус МДФ, h 80 мм, аналог: плинтус МДФ под окраску 80×16 мм, полуглянцевая | Tikkurila F497 «Рарег» | 2,9 м |
| О7 | потолок | окраска, Tikkurila Luja 7, матовая, подготовка Q3 | Tikkurila F497 «Рарег» | 15,2 м² |
| О13 | стены | окраска, Tikkurila Luja 7, шелковисто-матовая, подготовка К3 | Tikkurila F497 «Рарег» | 8 м² |

## Примечания


1. Размеры — в мм от чистовых поверхностей стен; условные обозначения и общие указания — лист 2.

| | | | | | |
|---|---|---|---|---|---|
| | | | | | Проект: Четырёхкомнатная квартира |
| | Лист | № док. | Подпись | Дата | |
| Дизайнер | Кырлан А.С. | | | 05.10.26 | Развёртка стены Б. Кухня (пом. 6) |


| Стадия | Лист | Листов |
|---|---|---|
| П | 63 | 111 |

выпуск 05.10.2026 № 05166c8858 · стр. 63 из 111

## Развёртка стены В

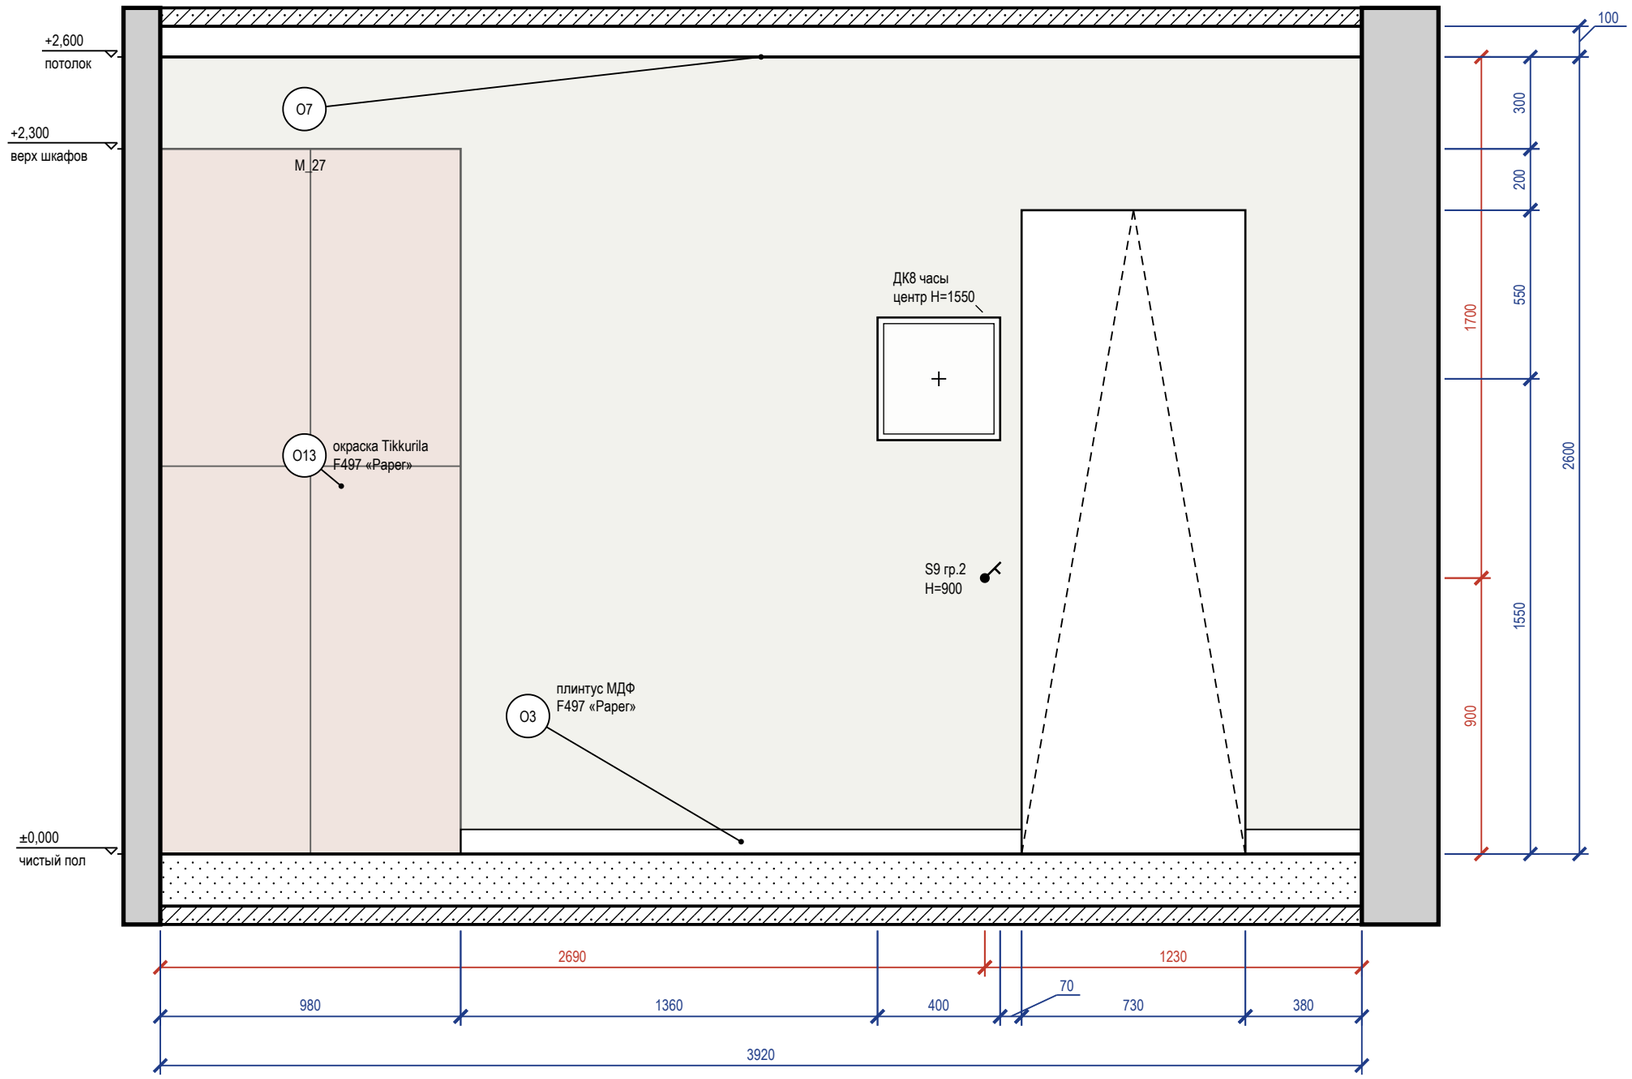


### Схема развёрток (М 1:100)

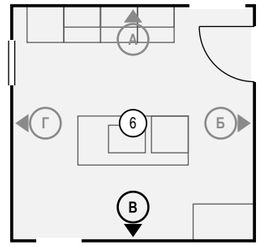


### Ведомость отделки (на листе)

| Марка | Поверхность | Материал, изделие | Цвет, код | Кол. |
|---|---|---|---|---|
| О3 | плинтус | плинтус МДФ, h 80 мм, аналог: плинтус МДФ под окраску 80×16 мм, полуглянцевая | Tikkurila F497 «Рарег» | 2,2 м |
| О7 | потолок | окраска, Tikkurila Luja 7, матовая, подготовка Q3 | Tikkurila F497 «Рарег» | 15,2 м² |
| О13 | стены | окраска, Tikkurila Luja 7, шелковисто-матовая, подготовка К3 | Tikkurila F497 «Рарег» | 8,7 м² |

### Примечания


1. Размеры — в мм от чистовых поверхностей стен; условные обозначения и общие указания — лист 2.
2. Картины и зеркала крепить к основанию по паспорту изделия (закладные и анкеры — в перечне скрытых работ); крест — ось центра предмета.

| | | | | | |
|---|---|---|---|---|---|
| | | | | | Проект: Четырёхкомнатная квартира |
| | Лист | № док. | Подпись | Дата | |
| Дизайнер | Кырлан А.С. | | | 05.10.26 | Развёртка стены В. Кухня (пом. 6) |


| Стадия | Лист | Листов |
|---|---|---|
| П | 64 | 111 |

выпуск 05.10.2026 № 05166c8858 · стр. 64 из 111

## Развёртка стены Г

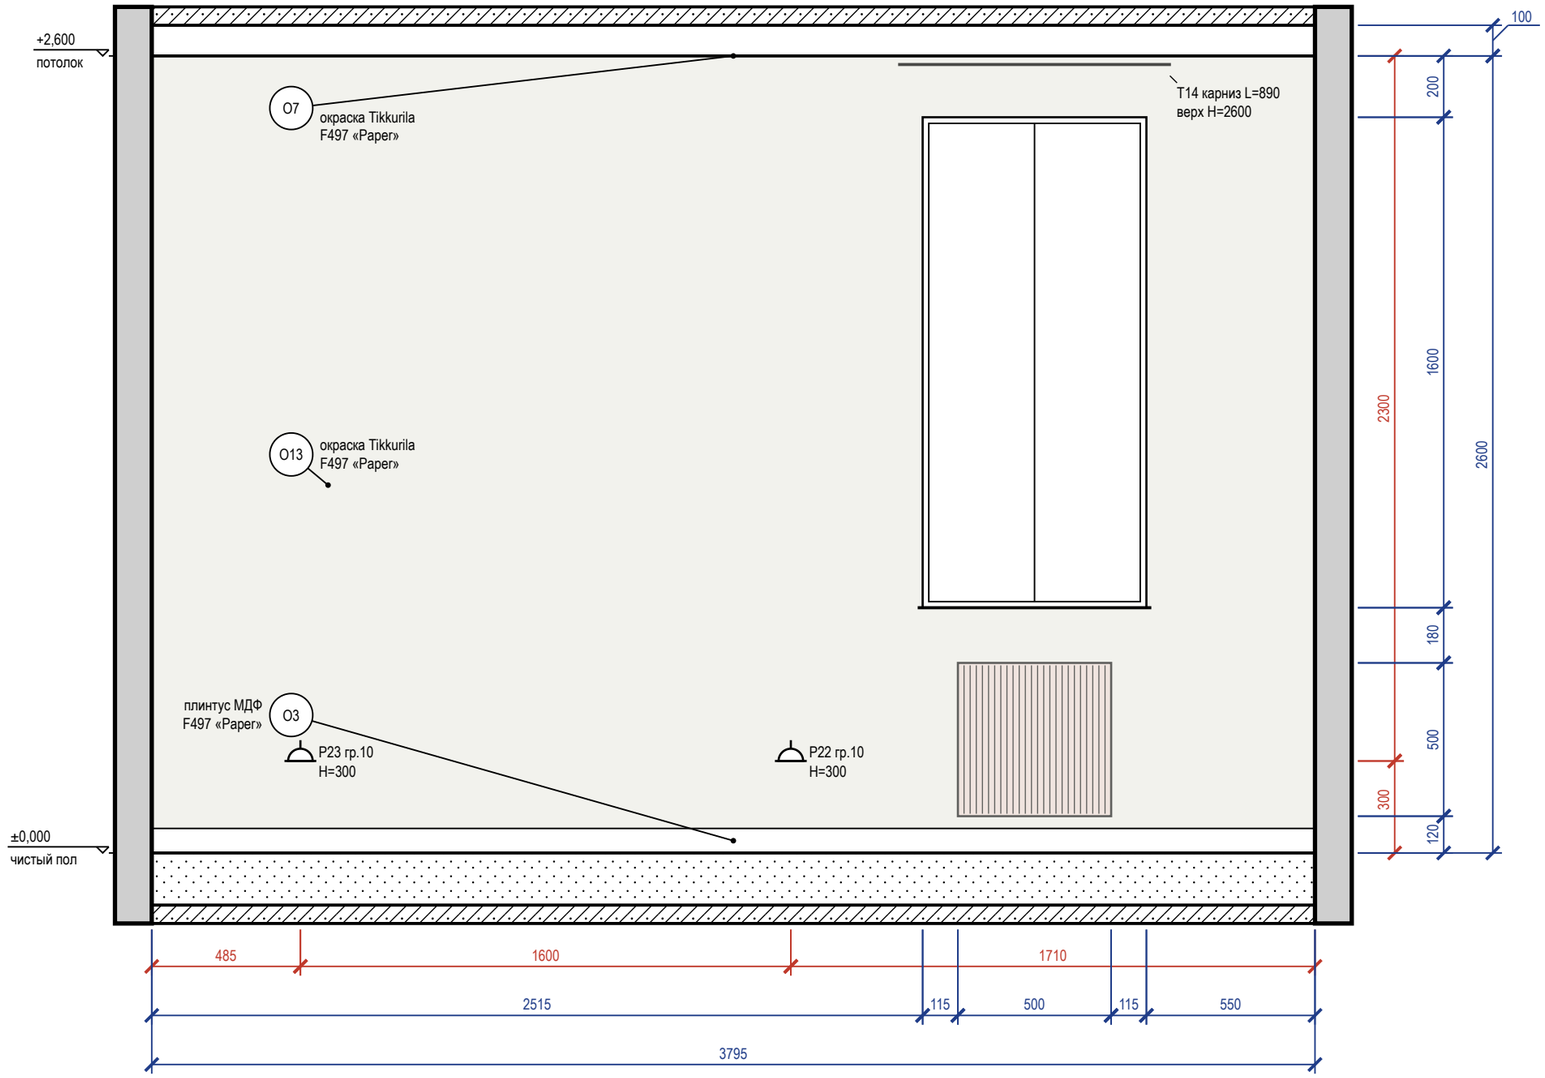


## Схема развёрток (М 1:100)

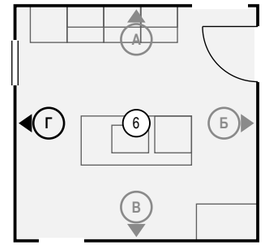


## Ведомость отделки (на листе)

| Марка | Поверхность | Материал, изделие | Цвет, код | Кол. |
|---|---|---|---|---|
| О3 | плинтус | плинтус МДФ, h 80 мм, аналог: плинтус МДФ под окраску 80×16 мм, полуглянцевая | Tikkurila F497 «Paper» | 3,8 м |
| О7 | потолок | окраска, Tikkurila Luja 7, матовая, подготовка Q3 | Tikkurila F497 «Paper» | 15,2 м² |
| О13 | стены | окраска, Tikkurila Luja 7, шелковисто-матовая, подготовка К3 | Tikkurila F497 «Paper» | 8,7 м² |

## Примечания

1. Размеры — в мм от чистовых поверхностей стен; условные обозначения и общие указания — лист 2.
2. Карнизы (шины) — по ведомости текстиля декоратора; длина L и верх H — по развёртке, крепление — до окраски потолка.

| | | | | | |
|---|---|---|---|---|---|
| | | | | | Проект: Четырёхкомнатная квартира |
| | Лист | № док. | Подпись | Дата | Развёртка стены Г. Кухня (пом. 6) |
| Дизайнер | Кырлан А.С. | | | 05.10.26 | |

| Стадия | Лист | Листов |
|---|---|---|
| П | 65 | 111 |

выпуск 05.10.2026 № 05166c8858 · стр. 65 из 111




| | | | | | |
|---|---|---|---|---|---|
| | | | | | Проект: Четырёхкомнатная квартира |
| | Лист | № док. | Подпись | Дата | |
| Дизайнер | Кырлан А.С. | | | 05.10.26 | Визуализация: Прихожая-коридор |


| Стадия | Лист | Листов |
|---|---|---|
| П | 66 | 111 |

выпуск 05.10.2026 № 0516c8858 · стр. 66 из 111

## Развёртка стены А

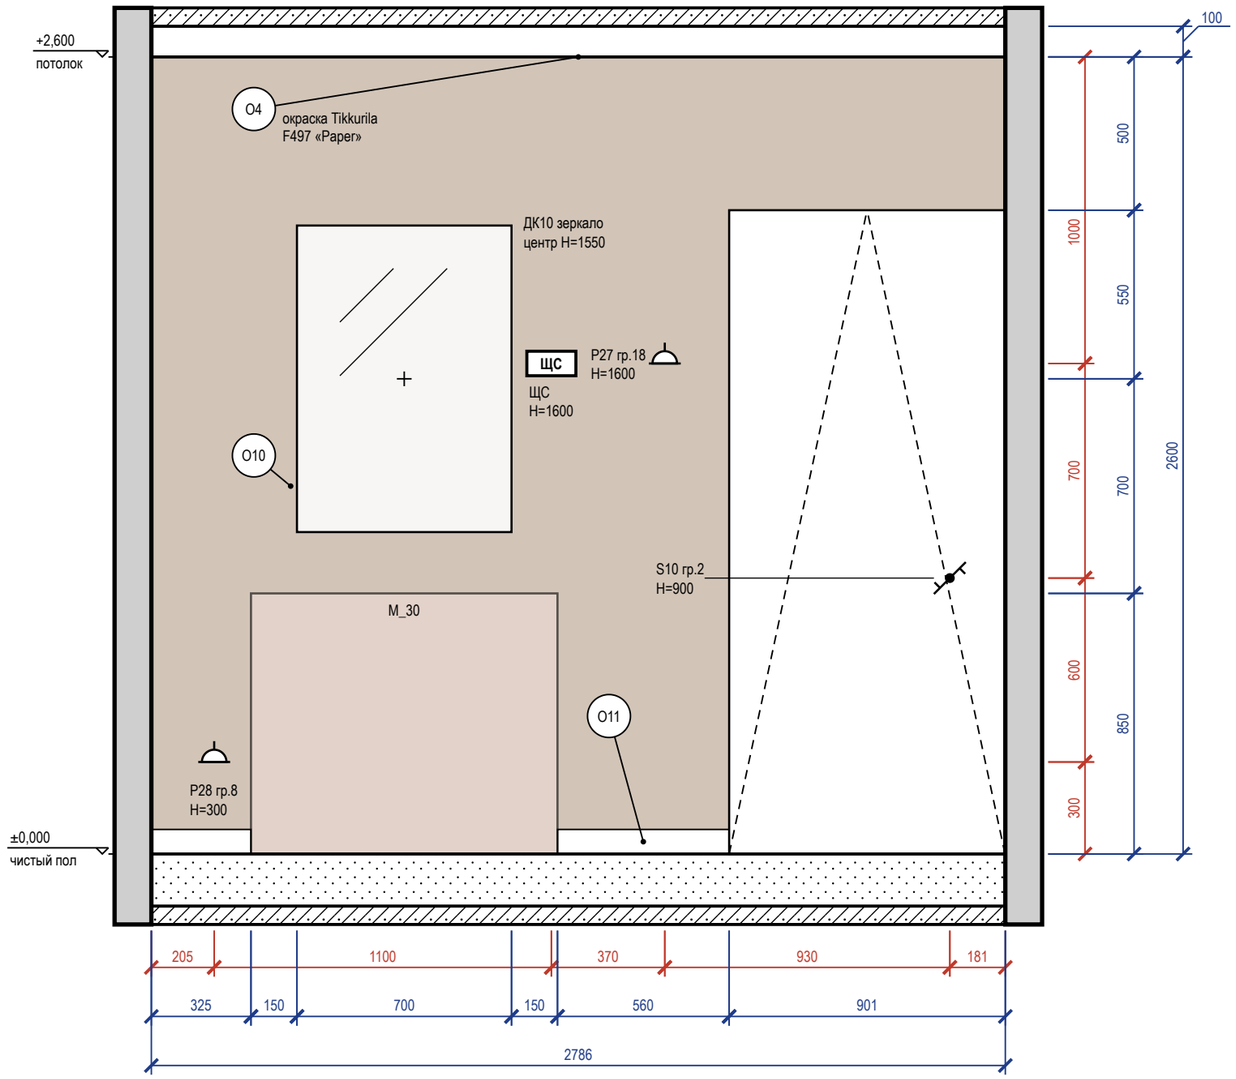


## Схема развёрток (М 1:100)

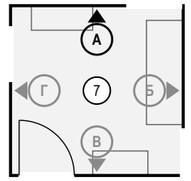


## Ведомость отделки (на листе)

| Марка | Поверхность | Материал, изделие | Цвет, код | Кол. |
|---|---|---|---|---|
| О4 | потолок | окраска, Tikkurila Anti-Reflex 2, глубокоматовая, подготовка Q3 | Tikkurila F497 «Paper» | 7,8 м² |
| О10 | стены | окраска, Tikkurila Optiva 20 Semimatt, шелковисто-матовая, подготовка К3 | Tikkurila J484 «Castle» | 5,4 м² |
| О11 | плинтус | плинтус МДФ, h 80 мм, аналог: плинтус МДФ под окраску 80×16 мм, полуглянцевая | Tikkurila J484 «Castle» | 0,9 м |

Визуализация этой стены — лист 66



### Примечания


1. Размеры — в мм от чистовых поверхностей стен; условные обозначения и общие указания — лист 2.
2. Картины и зеркала крепить к основанию по паспорту изделия (закладные и анкеры — в перечне скрытых работ); крест — ось центра предмета.

| | | | | | |
|---|---|---|---|---|---|
| | | | | | Проект: Четырёхкомнатная квартира |
| | Лист | № док. | Подпись | Дата | Развёртка стены А. Прихожая-коридор (пом. 7) |
| Дизайнер | Кырлан А.С. | | | 05.10.26 | |


| Стадия | Лист | Листов |
|---|---|---|
| П | 67 | 111 |

выпуск 05.10.2026 № 05166c8858 · стр. 67 из 111

## Развёртка стены Б

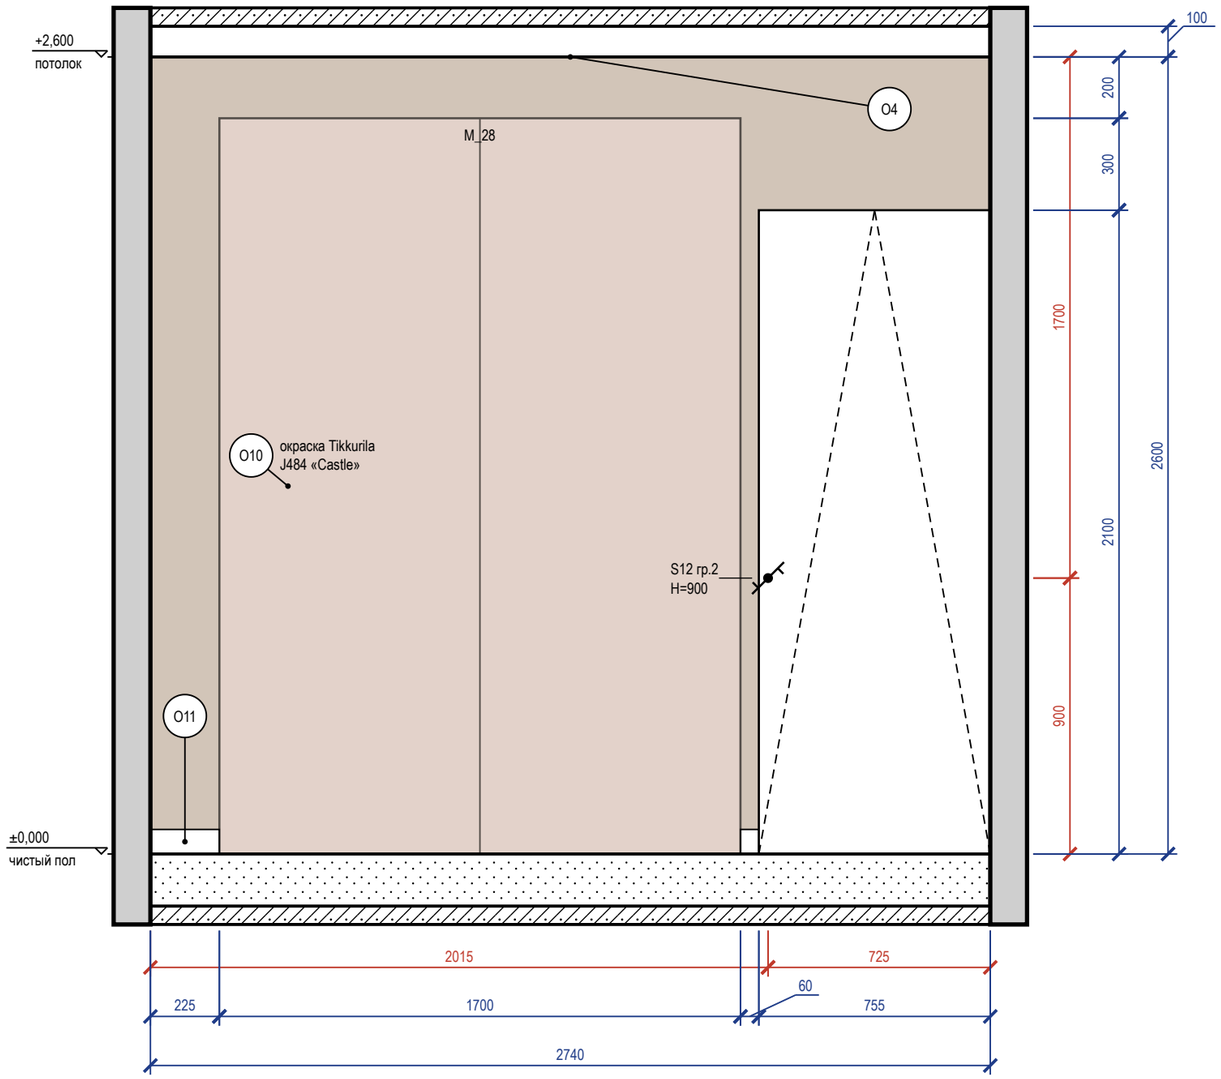


## Схема развёрток (М 1:100)

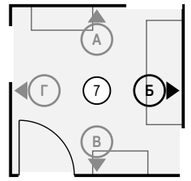


## Ведомость отделки (на листе)

| Марка | Поверхность | Материал, изделие | Цвет, код | Кол. |
|---|---|---|---|---|
| О4 | потолок | окраска, Tikkurila Anti-Reflex 2, глубокоматовая, подготовка Q3 | Tikkurila F497 «Paper» | 7,8 м² |
| О10 | стены | окраска, Tikkurila Optiva 20 Semimatt, шелковисто-матовая, подготовка К3 | Tikkurila J484 «Castle» | 5,5 м² |
| О11 | плинтус | плинтус МДФ, h 80 мм, аналог: плинтус МДФ под окраску 80×16 мм, полуглянцевая | Tikkurila J484 «Castle» | 0,3 м |

## Примечания


1. Размеры — в мм от чистовых поверхностей стен; условные обозначения и общие указания — лист 2.
2. Дверь заходит за угол помещения: на развёртке показана видимая часть проёма 770 из 900 мм — проверить привязку двери в модели.

| | | | | | |
|---|---|---|---|---|---|
| | | | | | Проект: Четырёхкомнатная квартира |
| | Лист | № док. | Подпись | Дата | Развёртка стены Б. Прихожая-коридор (пом. 7) |
| Дизайнер | Кырлан А.С. | | | 05.10.26 | |


| Стадия | Лист | Листов |
|---|---|---|
| П | 68 | 111 |

выпуск 05.10.2026 № 05166c8858 · стр. 68 из 111

## Развёртка стены В

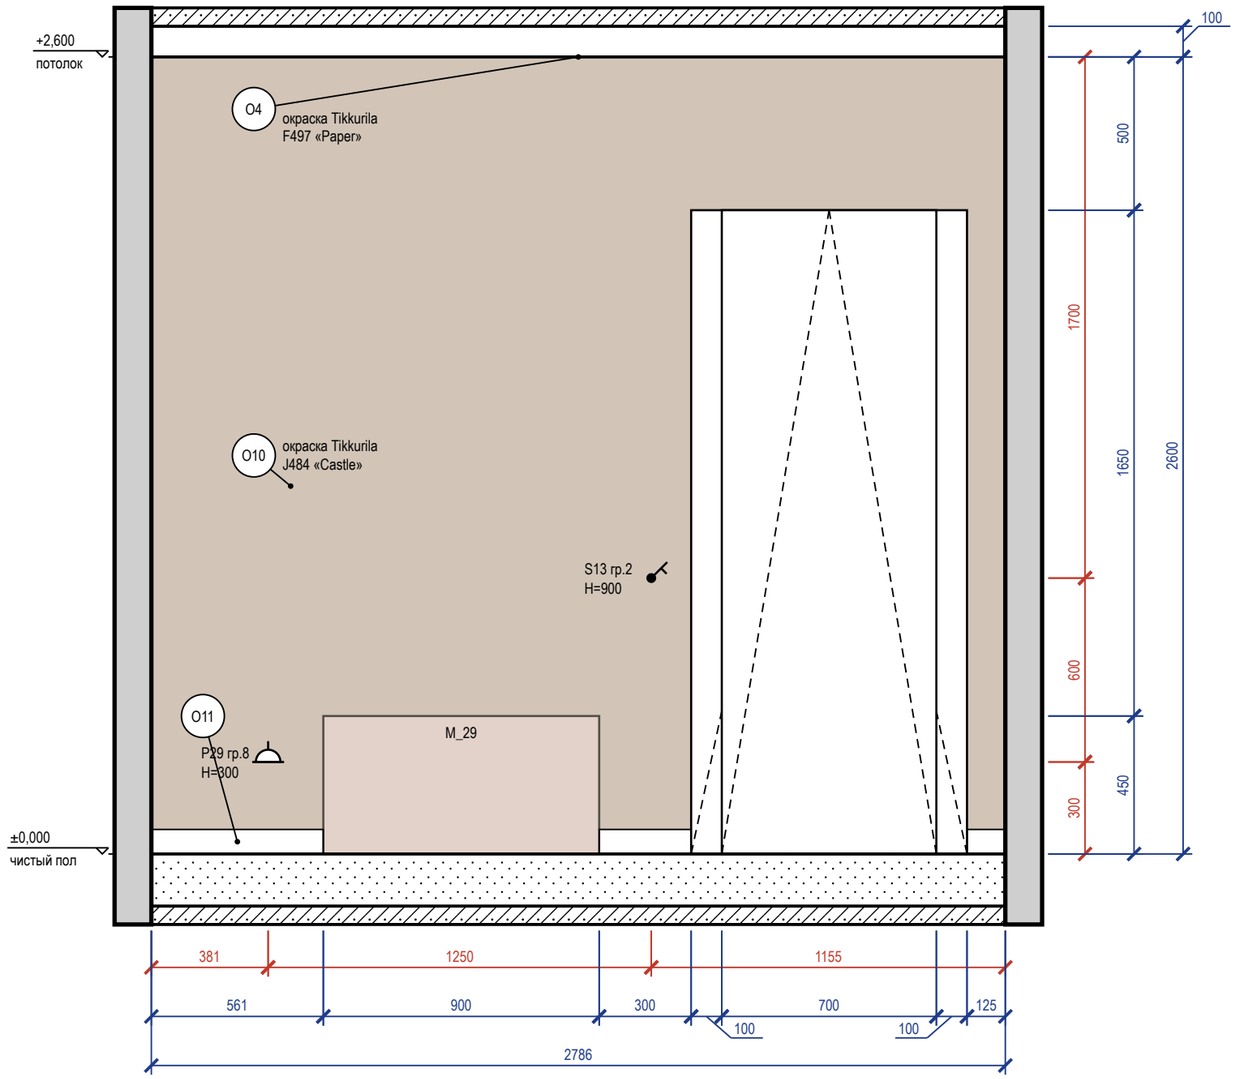


## Схема развёрток (М 1:100)

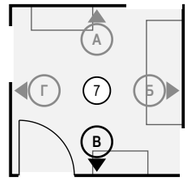


## Ведомость отделки (на листе)

| Марка | Поверхность | Материал, изделие | Цвет, код | Кол. |
|---|---|---|---|---|
| О4 | потолок | окраска, Tikkurila Anti-Reflex 2, глубокоматовая, подготовка Q3 | Tikkurila F497 «Paper» | 7,8 м² |
| О10 | стены | окраска, Tikkurila Optiva 20 Semimatt, шелковисто-матовая, подготовка К3 | Tikkurila J484 «Castle» | 3,9 м² |
| О11 | плинтус | плинтус МДФ, h 80 мм, аналог: плинтус МДФ под окраску 80×16 мм, полуглянцевая | Tikkurila J484 «Castle» | 1 м |

## Примечания


1. Размеры — в мм от чистовых поверхностей стен; условные обозначения и общие указания — лист 2.

| | | | | | |
|---|---|---|---|---|---|
| | | | | | Проект: Четырёхкомнатная квартира |
| | Лист | № док. | Подпись | Дата | Развёртка стены В. Прихожая-коридор (пом. 7) |
| Дизайнер | Кырлан А.С. | | | 05.10.26 | |


| Стадия | Лист | Листов |
|---|---|---|
| П | 69 | 111 |

выпуск 05.10.2026 № 05166c8858 · стр. 69 из 111

## Развёртка стены Г

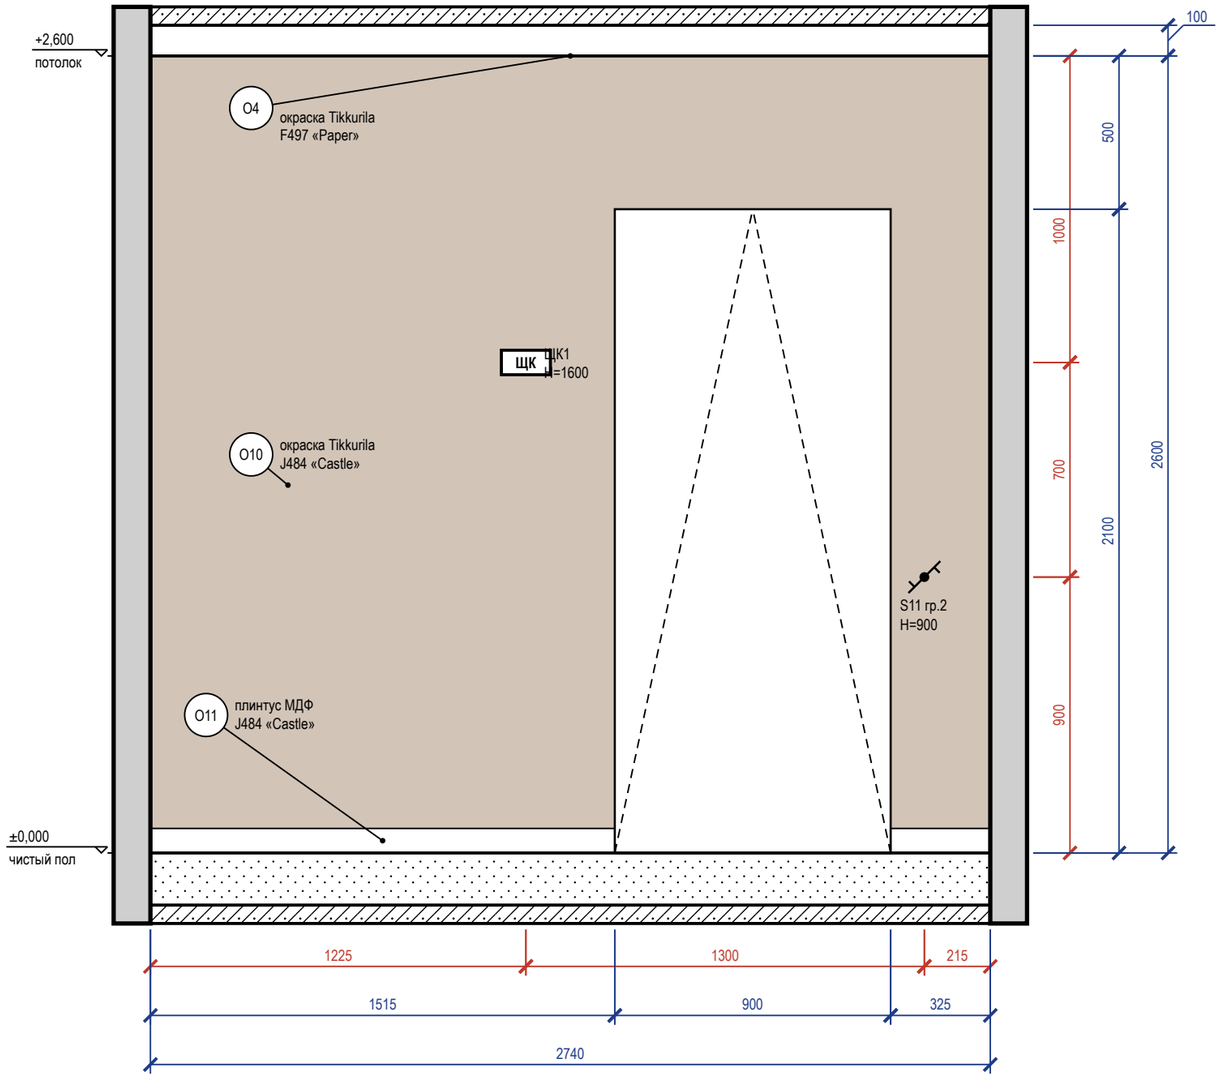


## Схема развёрток (М 1:100)

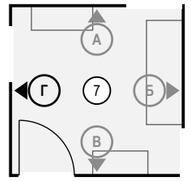


## Ведомость отделки (на листе)

| Марка | Поверхность | Материал, изделие | Цвет, код | Кол. |
|---|---|---|---|---|
| О4 | потолок | окраска, Tikkurila Anti-Reflex 2, глубокоматовая, подготовка Q3 | Tikkurila F497 «Paper» | 7,8 м² |
| О10 | стены | окраска, Tikkurila Optiva 20 Semimatt, шелковисто-матовая, подготовка К3 | Tikkurila J484 «Castle» | 5,2 м² |
| О11 | плинтус | плинтус МДФ, h 80 мм, аналог: плинтус МДФ под окраску 80×16 мм, полуглянцевая | Tikkurila J484 «Castle» | 1,8 м |

### Примечания

1. Размеры — в мм от чистовых поверхностей стен; условные обозначения и общие указания — лист 2.

| | | | | | |
|---|---|---|---|---|---|
| | | | | | Проект: Четырёхкомнатная квартира |
| | Лист | № док. | Подпись | Дата | Развёртка стены Г. Прихожая-коридор (пом. 7) |
| Дизайнер | Кырлан А.С. | | | 05.10.26 | |

| Стадия | Лист | Листов |
|---|---|---|
| П | 70 | 111 |

выпуск 05.10.2026 № 05166c8858 · стр. 70 из 111




| | | | | | |
|---|---|---|---|---|---|
| | | | | | Проект: Четырёхкомнатная квартира |
| | Лист | № док. | Подпись | Дата | |
| Дизайнер | Кырлан А.С. | | | 05.10.26 | Визуализация: Гардеробная 2 |


| Стадия | Лист | Листов |
|---|---|---|
| П | 71 | 111 |

выпуск 05.10.2026 № 05166c8858 · стр. 71 из 111


## Развёртка стены А

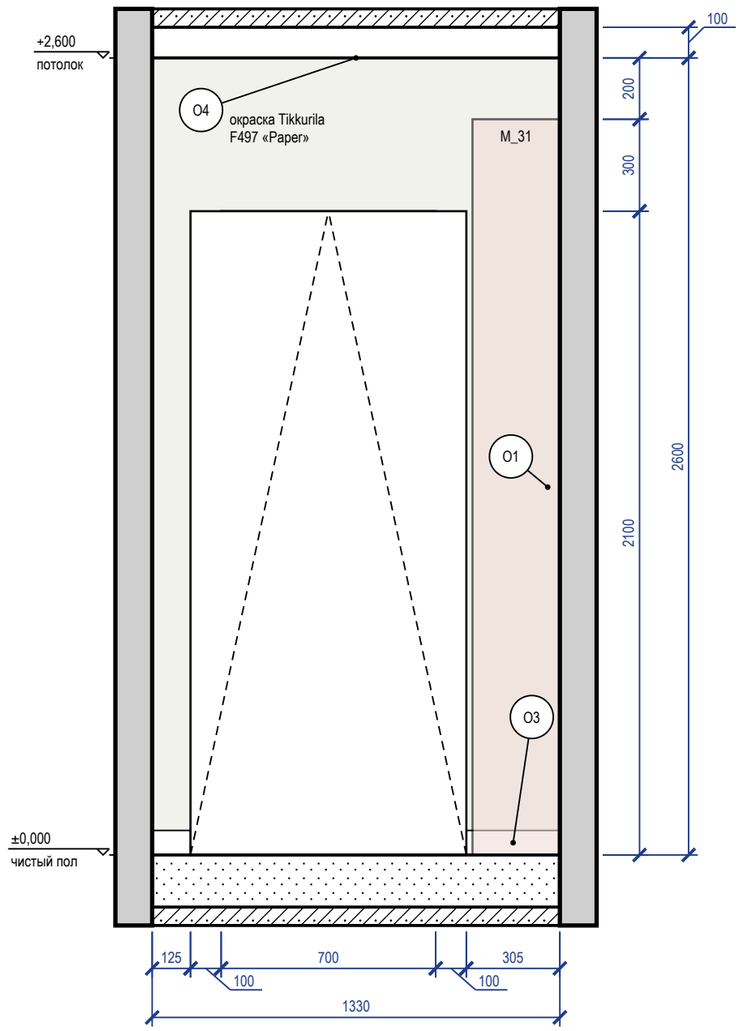


## Развёртка стены Б

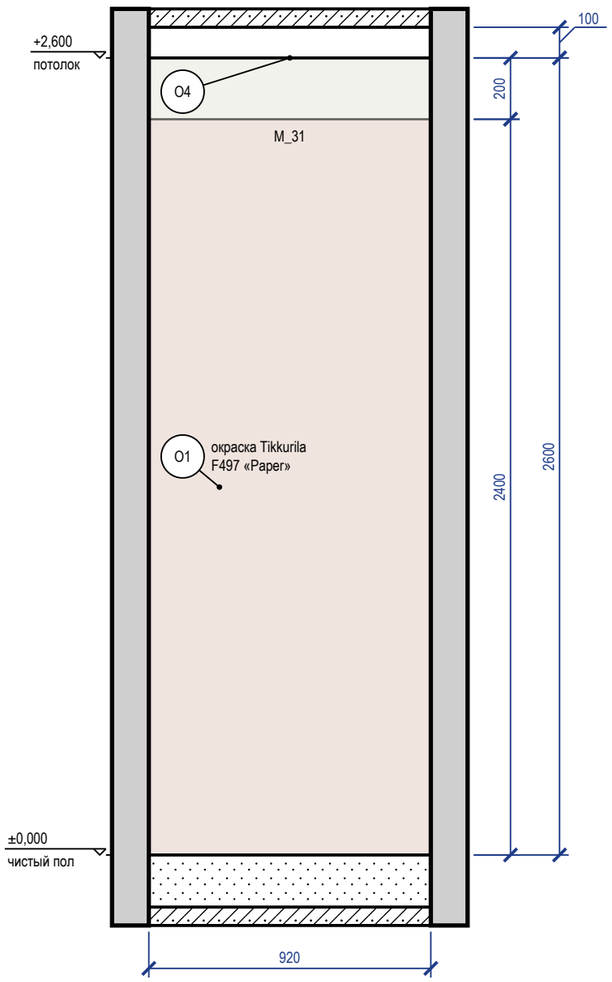


## Развёртка стены В

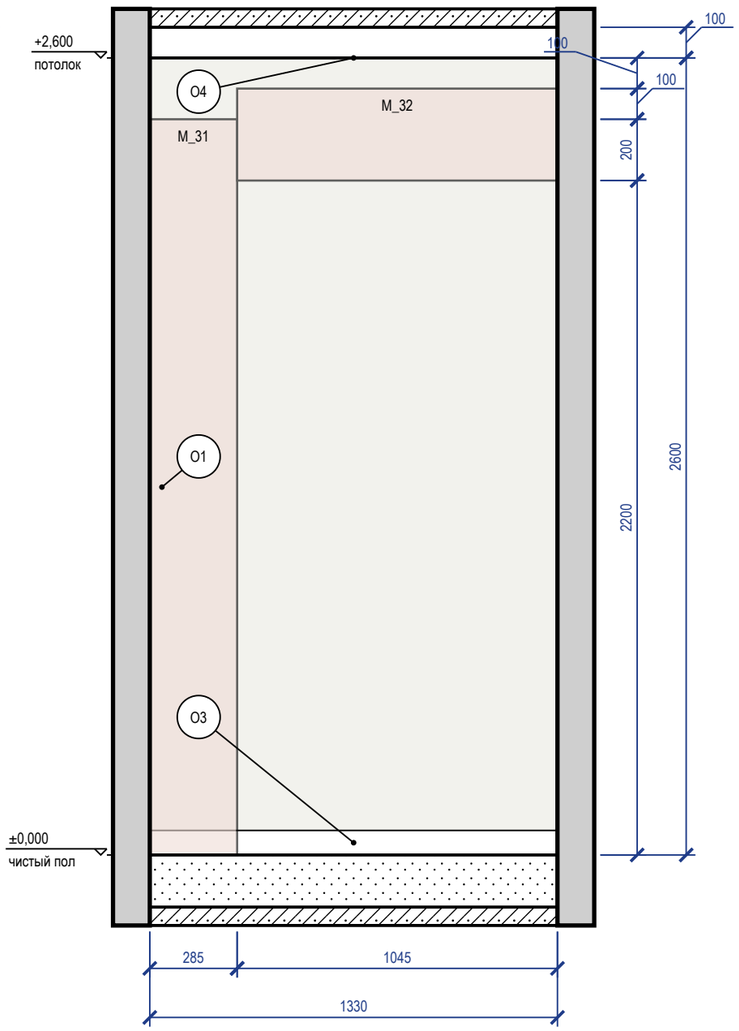


### Схема развёрток (М 1:100)




### Ведомость отделки (на листе)

| Марка | Поверхность | Материал, изделие | Цвет, код | Кол. |
|---|---|---|---|---|
| О1 | стены | окраска, Tikkurila Optiva 5 Matt, матовая, подготовка К3 | Tikkurila F497 «Paper» | 5,9 м² |
| О3 | плинтус | плинтус МДФ, h 80 мм, аналог: плинтус МДФ под окраску 80×16 мм, полуглянцевая | Tikkurila F497 «Paper» | 1,8 м |
| О4 | потолок | окраска, Tikkurila Anti-Reflex 2, глубокоматовая, подготовка Q3 | Tikkurila F497 «Paper» | 1,3 м² |

Визуализация этой стены — лист 71



### Примечания


1. Размеры — в мм от чистовых поверхностей стен; условные обозначения и общие указания — лист 2.

| | | | | | |
|---|---|---|---|---|---|
| | | | | | Проект: Четырёхкомнатная квартира |
| | Лист | № док. | Подпись | Дата | Развёртки стен А, Б, В. Гардеробная 2 (пом. 8) |
| Дизайнер | Кырлан А.С. | | | 05.10.26 | |


| Стадия | Лист | Листов |
|---|---|---|
| П | 72 | 111 |

выпуск 05.10.2026 № 05166c8858 · стр. 72 из 111

## Развёртка стены Г

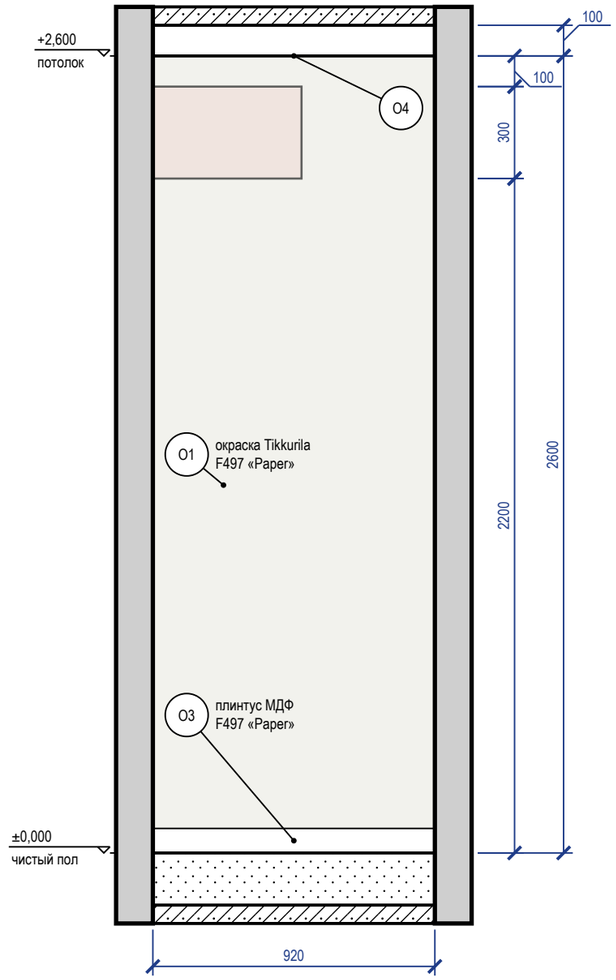


## Схема развёрток (М 1:100)

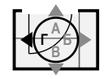


## Ведомость отделки (на листе)

| Марка | Поверхность | Материал, изделие | Цвет, код | Кол. |
|---|---|---|---|---|
| О1 | стены | окраска, Tikkurila Optiva 5 Matt, матовая, подготовка К3 | Tikkurila F497 «Paper» | 2,4 м² |
| О3 | плинтус | плинтус МДФ, h 80 мм, аналог: плинтус МДФ под окраску 80×16 мм, полуглянцевая | Tikkurila F497 «Paper» | 0,9 м |
| О4 | потолок | окраска, Tikkurila Anti-Reflex 2, глубокоматовая, подготовка Q3 | Tikkurila F497 «Paper» | 1,3 м² |

## Примечания

1. Размеры — в мм от чистовых поверхностей стен; условные обозначения и общие указания — лист 2.

| | Лист | № док. | Подпись | Дата |
|---|---|---|---|---|
| Дизайнер | Кырлан А.С. | | | 05.10.26 |

Проект: Четырёхкомнатная квартира

Развёртка стены Г. Гардеробная 2 (пом. 8)

| Стадия | Лист | Листов |
|---|---|---|
| П | 73 | 111 |

выпуск 05.10.2026 № 05166c8858 · стр. 73 из 111



| | | | | | |
|---|---|---|---|---|---|
| | | | | | Проект: Четырёхкомнатная квартира |
| | Лист | № док. | Подпись | Дата | |
| Дизайнер | Кырлан А.С. | | | 05.10.26 | Визуализация: Детская 2 |

| Стадия | Лист | Листов |
|---|---|---|
| П | 74 | 111 |

выпуск 05.10.2026 № 0516c8858 · стр. 74 из 111




| | | | | | |
|---|---|---|---|---|---|
| | | | | | Проект: Четырёхкомнатная квартира |
| | Лист | № док. | Подпись | Дата | |
| Дизайнер | Кырлан А.С. | | | 05.10.26 | Визуализация: Детская 2 |


| Стадия | Лист | Листов |
|---|---|---|
| П | 75 | 111 |

выпуск 05.10.2026 № 05166c8858 · стр. 75 из 111

## Развёртка стены А

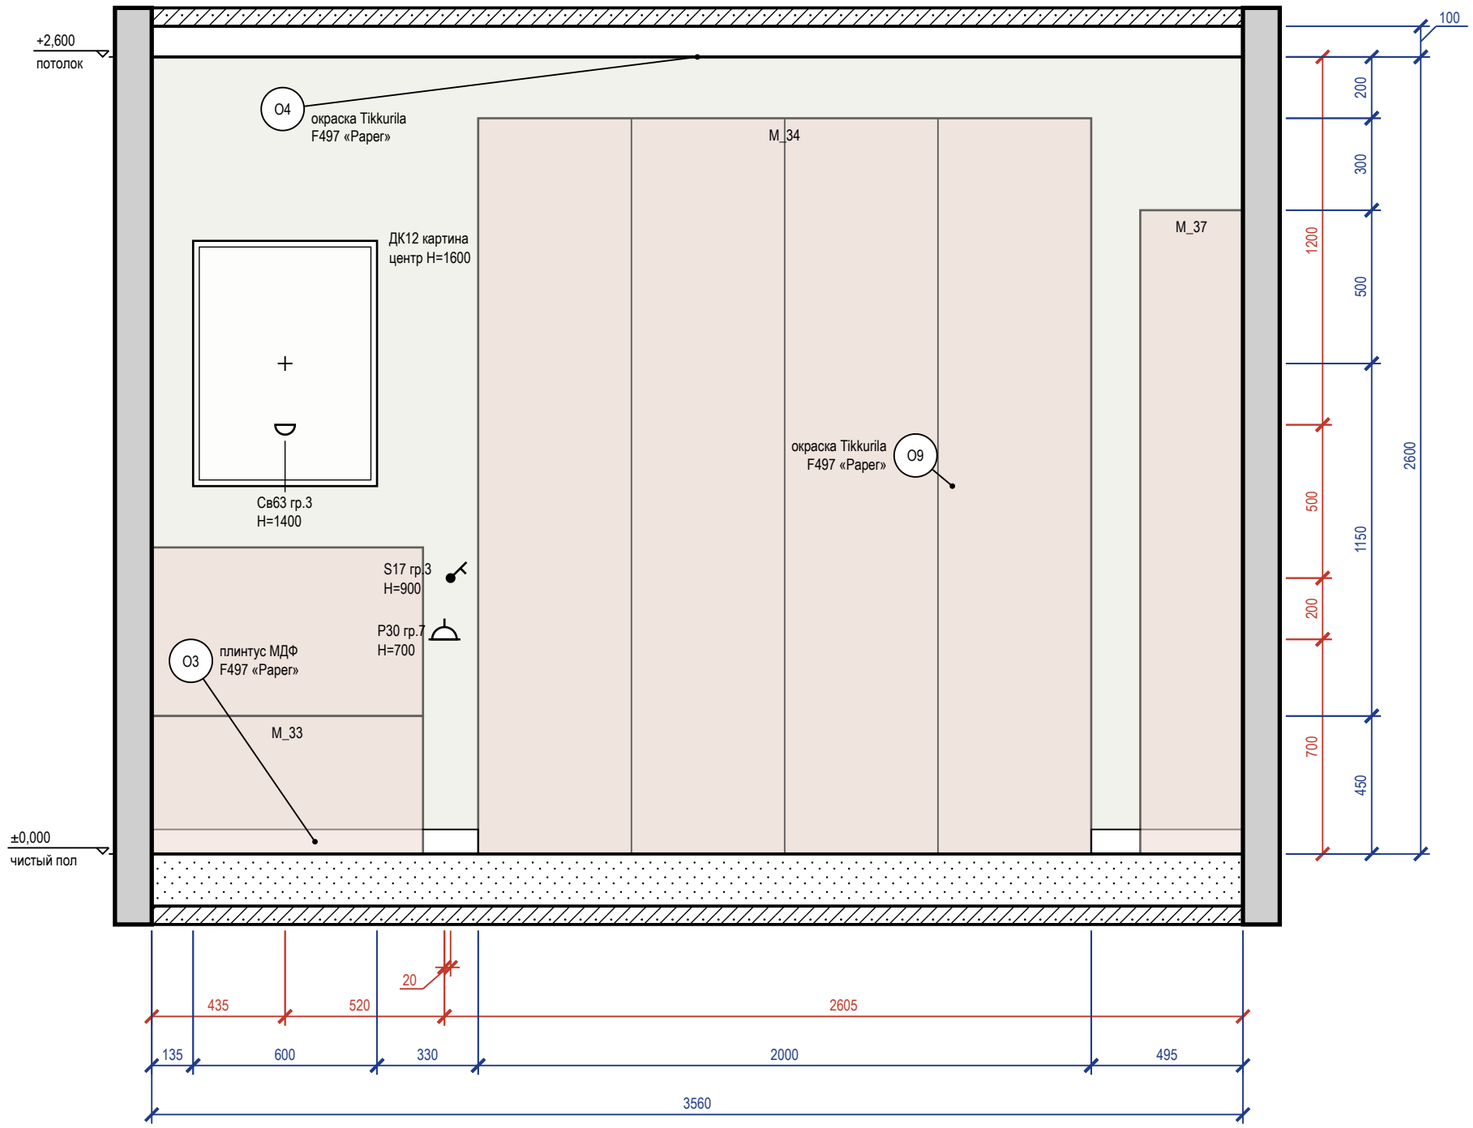


## Схема развёрток (М 1:100)

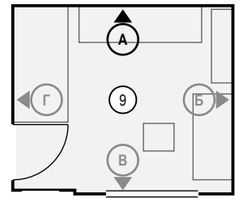


## Ведомость отделки (на листе)

| Марка | Поверхность | Материал, изделие | Цвет, код | Кол. |
|---|---|---|---|---|
| О3 | плинтус | плинтус МДФ, h 80 мм, аналог: плинтус МДФ под окраску 80×16 мм, полуглянцевая | Tikkurila F497 «Paper» | 1,6 м |
| О4 | потолок | окраска, Tikkurila Anti-Reflex 2, глубокоматовая, подготовка Q3 | Tikkurila F497 «Paper» | 11 м² |
| О9 | стены | окраска, Tikkurila Joker, шелковисто-матовая, подготовка К3 | Tikkurila F497 «Paper» | 9,3 м² |

Визуализация этой стены — лист 74



## Примечания


1. Размеры — в мм от чистовых поверхностей стен; условные обозначения и общие указания — лист 2.
2. Картины и зеркала крепить к основанию по паспорту изделия (закладные и анкеры — в перечне скрытых работ); крест — ось центра предмета.

| | | | | | |
|---|---|---|---|---|---|
| | | | | | Проект: Четырёхкомнатная квартира |
| | Лист | № док. | Подпись | Дата | |
| Дизайнер | Кырлан А.С. | | | 05.10.26 | Развёртка стены А. Детская 2 (пом. 9) |


| Стадия | Лист | Листов |
|---|---|---|
| П | 76 | 111 |

выпуск 05.10.2026 № 05166c8858 · стр. 76 из 111

## Развёртка стены Б

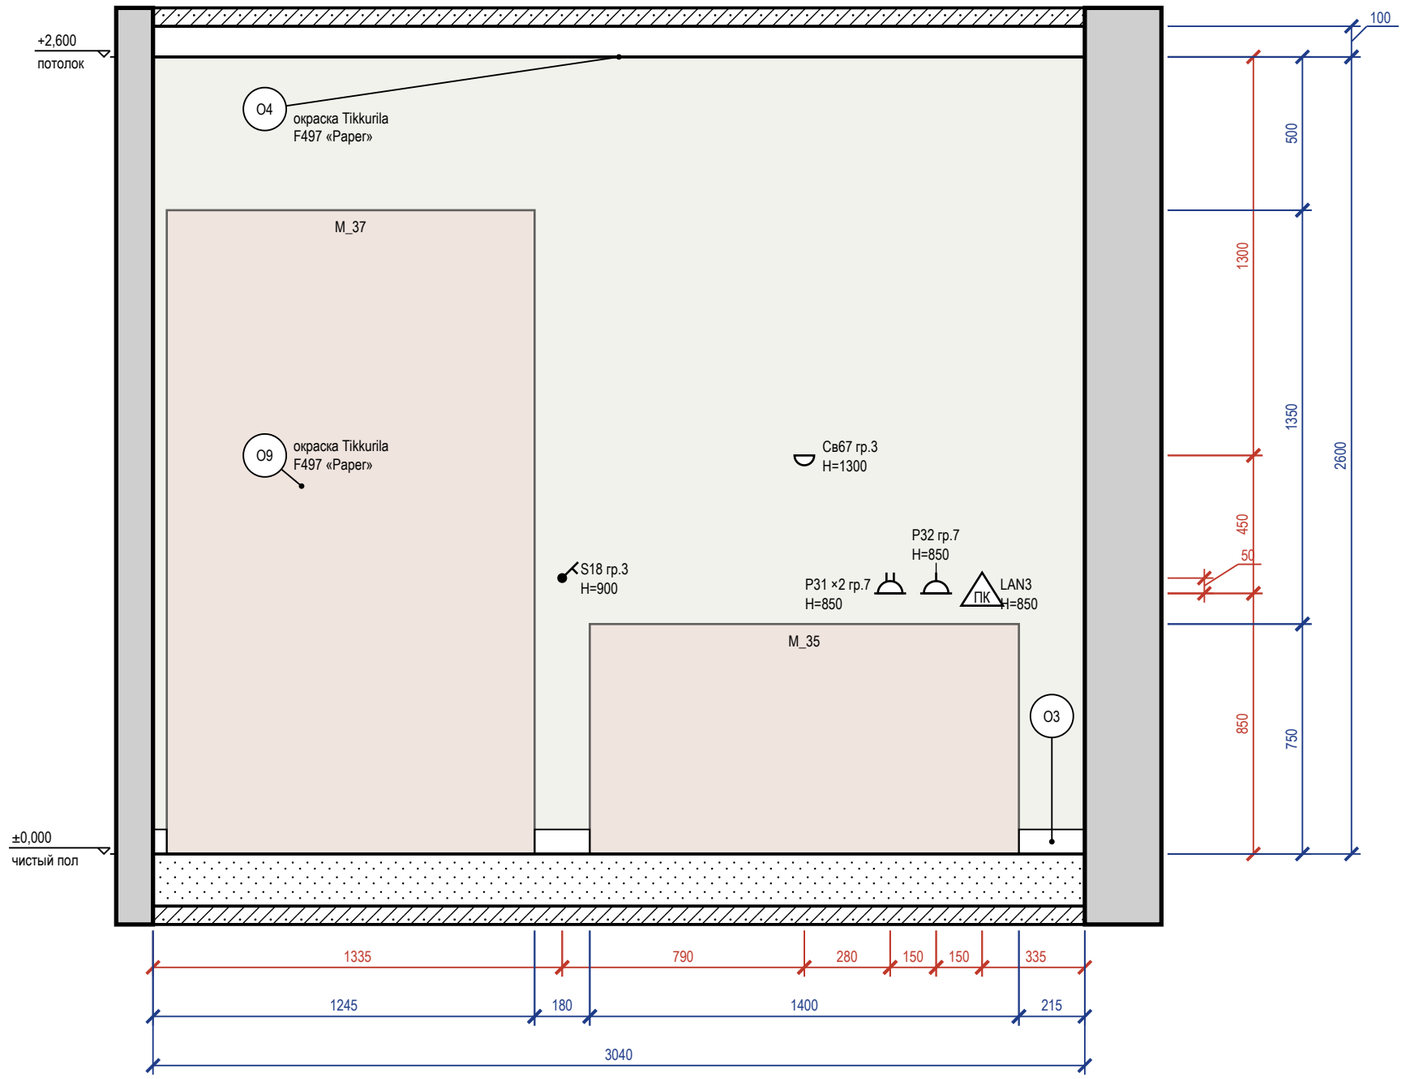


## Схема развёрток (М 1:100)

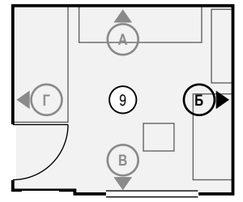


## Ведомость отделки (на листе)

| Марка | Поверхность | Материал, изделие | Цвет, код | Кол. |
|---|---|---|---|---|
| О3 | плинтус | плинтус МДФ, h 80 мм, аналог: плинтус МДФ под окраску 80×16 мм, полуглянцевая | Tikkurila F497 «Paper» | 0,4 м |
| О4 | потолок | окраска, Tikkurila Anti-Reflex 2, глубокоматовая, подготовка Q3 | Tikkurila F497 «Paper» | 11 м² |
| О9 | стены | окраска, Tikkurila Joker, шелковисто-матовая, подготовка К3 | Tikkurila F497 «Paper» | 7,9 м² |

### Примечания


1. Размеры — в мм от чистовых поверхностей стен; условные обозначения и общие указания — лист 2.

| | | | | | |
|---|---|---|---|---|---|
| | | | | | Проект: Четырёхкомнатная квартира |
| | Лист | № док. | Подпись | Дата | |
| Дизайнер | Кырлан А.С. | | | 05.10.26 | Развёртка стены Б. Детская 2 (пом. 9) |


| Стадия | Лист | Листов |
|---|---|---|
| П | 77 | 111 |

выпуск 05.10.2026 № 05166c8858 · стр. 77 из 111

## Развёртка стены В

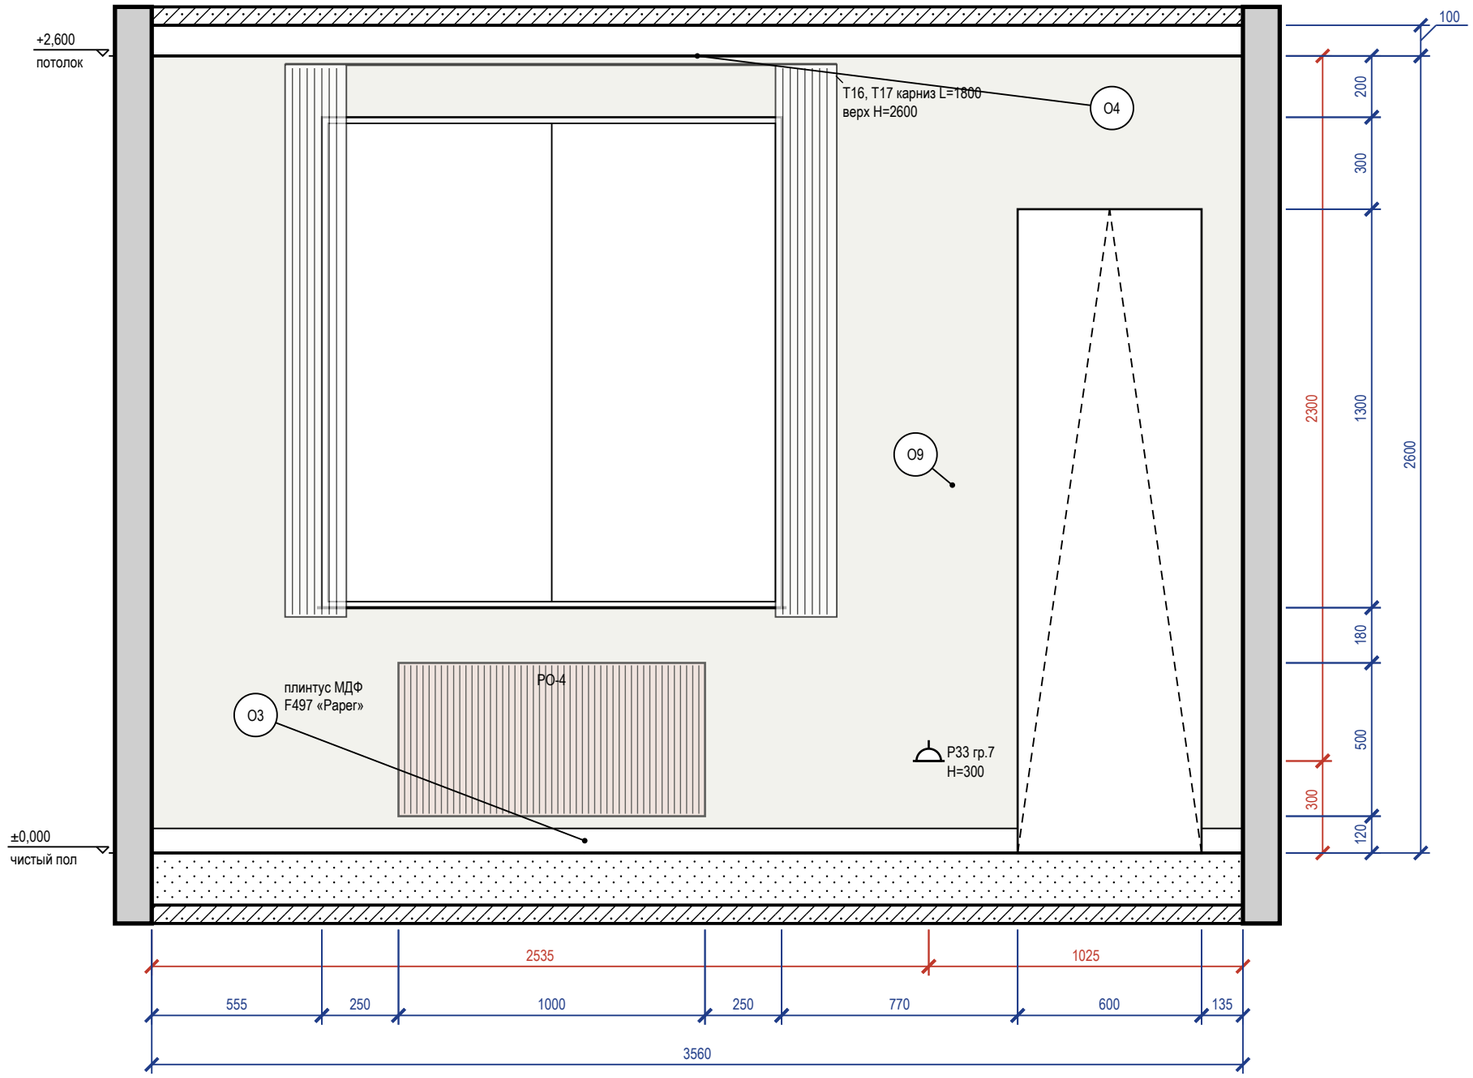


## Схема развёрток (М 1:100)

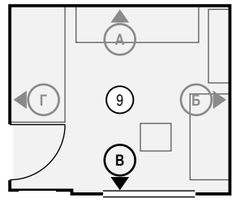


## Ведомость отделки (на листе)

| Марка | Поверхность | Материал, изделие | Цвет, код | Кол. |
|---|---|---|---|---|
| О3 | плинтус | плинтус МДФ, h 80 мм, аналог: плинтус МДФ под окраску 80×16 мм, полуглянцевая | Tikkurila F497 «Paperi» | 3 м |
| О4 | потолок | окраска, Tikkurila Anti-Reflex 2, глубокоматовая, подготовка Q3 | Tikkurila F497 «Paperi» | 11 м² |
| О9 | стены | окраска, Tikkurila Joker, шелковисто-матовая, подготовка К3 | Tikkurila F497 «Paperi» | 5,6 м² |

### Примечания


1. Размеры — в мм от чистовых поверхностей стен; условные обозначения и общие указания — лист 2.
2. Карнизы (шины) — по ведомости текстиля декоратора; длина L и верх H — по развёртке, крепление — до окраски потолка.

| | | | | | |
|---|---|---|---|---|---|
| | | | | | Проект: Четырёхкомнатная квартира |
| | Лист | № док. | Подпись | Дата | Развёртка стены В. Детская 2 (пом. 9) |
| Дизайнер | Кырлан А.С. | | | 05.10.26 | |


| Стадия | Лист | Листов |
|---|---|---|
| П | 78 | 111 |

выпуск 05.10.2026 № 05166c8858 · стр. 78 из 111

## Развёртка стены Г

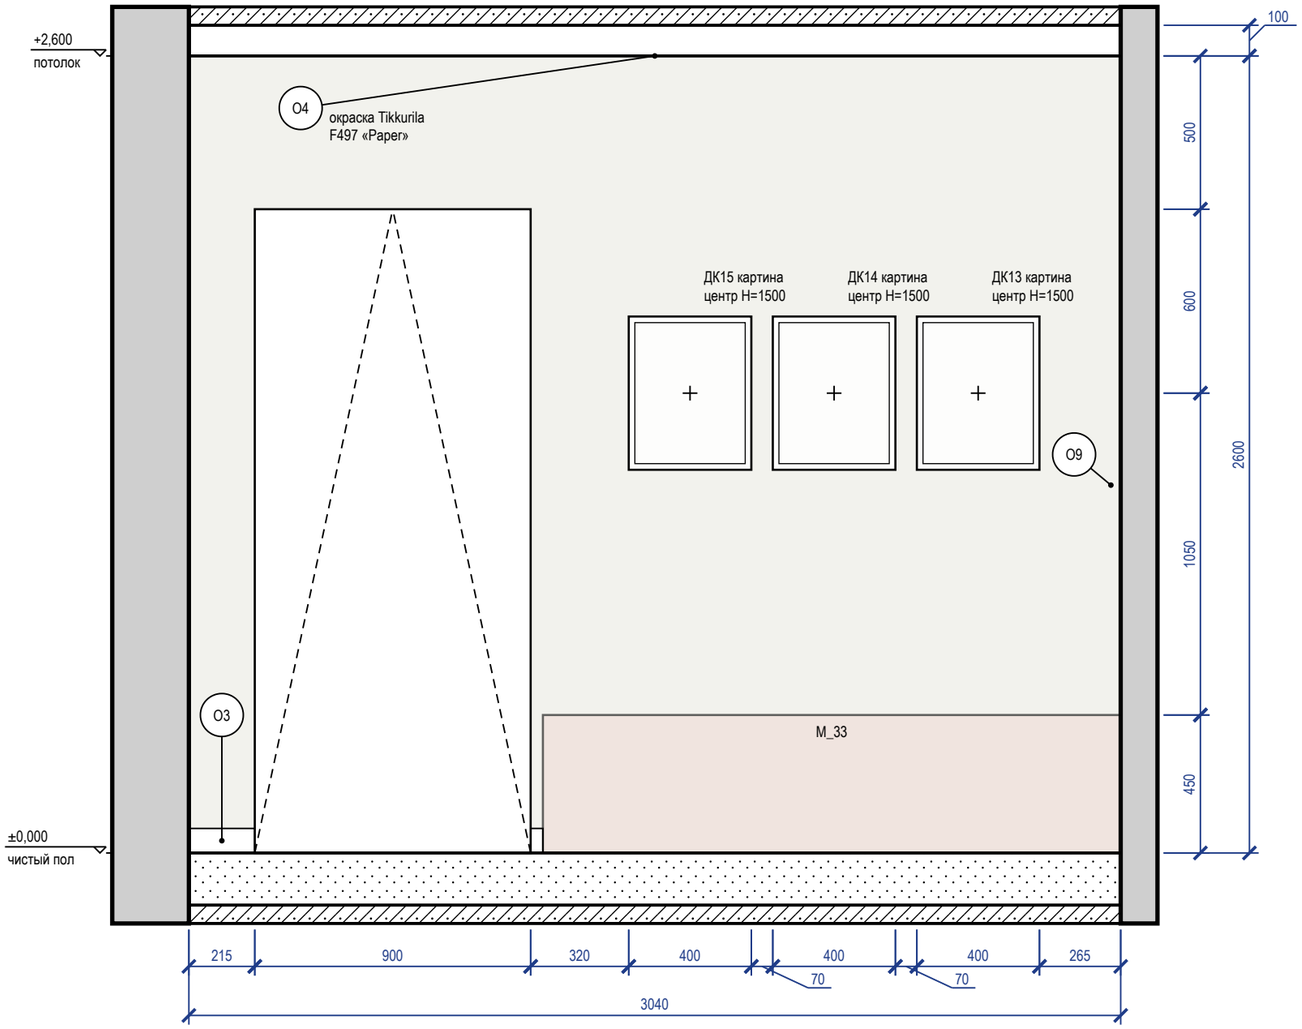


## Схема развёрток (М 1:100)

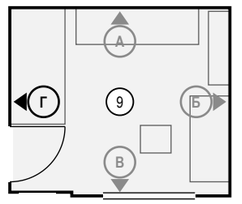


## Ведомость отделки (на листе)

| Марка | Поверхность | Материал, изделие | Цвет, код | Кол. |
|---|---|---|---|---|
| О3 | плинтус | плинтус МДФ, h 80 мм, аналог: плинтус МДФ под окраску 80×16 мм, полуглянцевая | Tikkurila F497 «Paper» | 0,3 м |
| О4 | потолок | окраска, Tikkurila Anti-Reflex 2, глубокоматовая, подготовка Q3 | Tikkurila F497 «Paper» | 11 м² |
| О9 | стены | окраска, Tikkurila Joker, шелковисто-матовая, подготовка К3 | Tikkurila F497 «Paper» | 6 м² |

Визуализация этой стены — лист 75



### Примечания

1. Размеры — в мм от чистовых поверхностей стен; условные обозначения и общие указания — лист 2.
2. Картины и зеркала крепить к основанию по паспорту изделия (закладные и анкеры — в перечне скрытых работ); крест — ось центра предмета.

| | Лист | № док. | Подпись | Дата |
|---|---|---|---|---|
| Дизайнер | Кырлан А.С. | | | 05.10.26 |

Проект: Четырёхкомнатная квартира

Развёртка стены Г. Детская 2 (пом. 9)

| Стадия | Лист | Листов |
|---|---|---|
| П | 79 | 111 |

выпуск 05.10.2026 № 05166c8858 · стр. 79 из 111




| | | | | | |
|---|---|---|---|---|---|
| | | | | | Проект: Четырёхкомнатная квартира |
| | Лист | № док. | Подпись | Дата | Визуализация санузла |
| Дизайнер | Кырлан А.С. | | | 05.10.26 | |


| Стадия | Лист | Листов |
|---|---|---|
| П | 80 | 111 |

выпуск 05.10.2026 № 05166c8858 · стр. 80 из 111

## Развёртка стены А

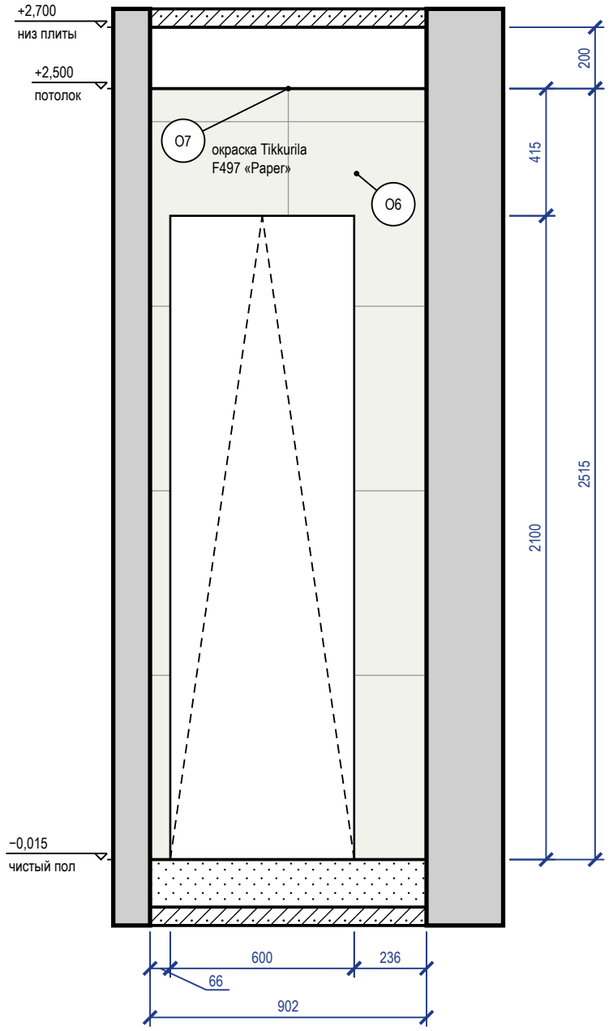


## Развёртка стены Б

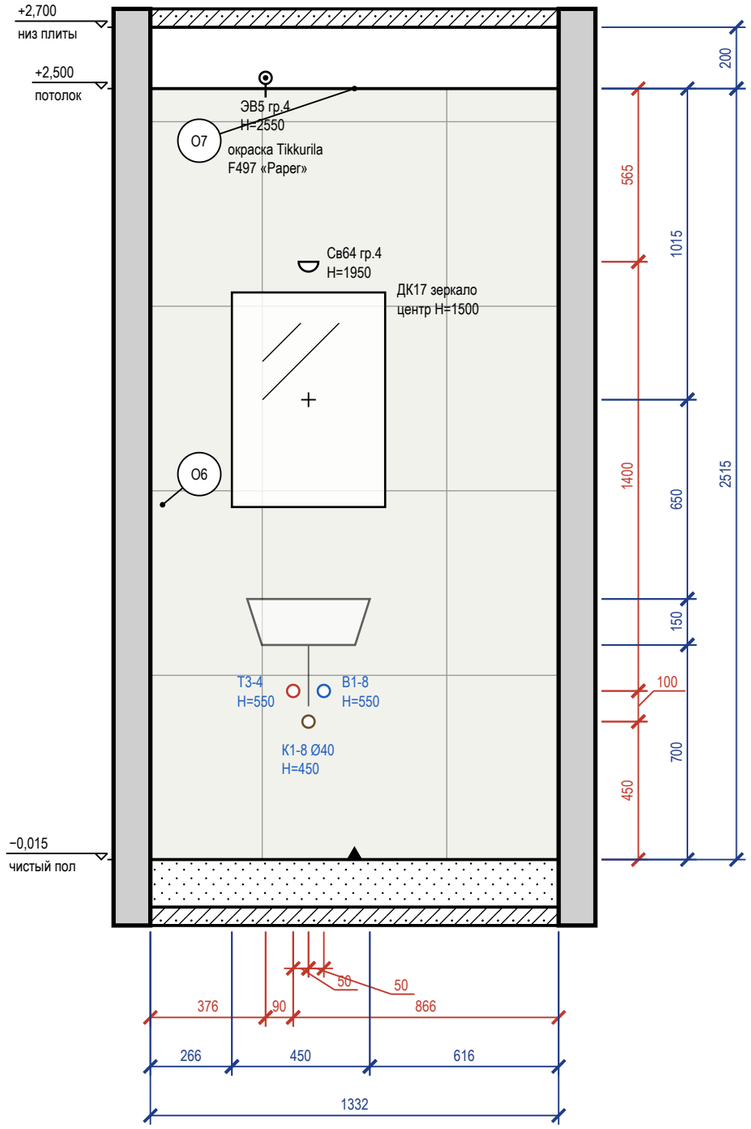


## Схема развёрток (М 1:100)




## Ведомость отделки (на листе)

| Марка | Поверхность | Материал, изделие | Цвет, код | Кол. |
|---|---|---|---|---|
| О6 | стены | облицовка плиткой, 600×600×9 мм, аналог: керамогранит матовый, тон F497, затирка CG2WA | #F1F1EC «тон Paper F497» | 4,4 м² |
| О7 | потолок | окраска, Tikkurila Luja 7, матовая, подготовка Q3 | Tikkurila F497 «Paper» | 1,3 м² |

## Примечания


1. Размеры — в мм от чистовых поверхностей стен; условные обозначения и общие указания — лист 2.
2. Облицовка — по сетке швов 2 мм, раскладка от оси стены (треугольник у пола); подрезки — по листу раскладки плитки.
3. Гидроизоляция в 2 слоя, заход на стены 200 мм — до облицовки, с актом скрытых работ и тестом проливом (узел — на листе узлов).
4. Картины и зеркала крепить к основанию по паспорту изделия (закладные и анкеры — в перечне скрытых работ); крест — ось центра предмета.
5. Линии узора (швы плитки, складки штор, рёбра радиаторов) прерываются у знаков и выносок — просвет между линиями не менее 0,7 мм.

| | | | | | |
|---|---|---|---|---|---|
| | | | | | Проект: Четырёхкомнатная квартира |
| | Лист | № док. | Подпись | Дата | |
| Дизайнер | Кырлан А.С. | | | 05.10.26 | Развёртки стен А, Б. Санузел (пом. 10) |


| Стадия | Лист | Листов |
|---|---|---|
| П | 81 | 111 |

выпуск 05.10.2026 № 0516ec8858 · стр. 81 из 111

## Развёртка стены В

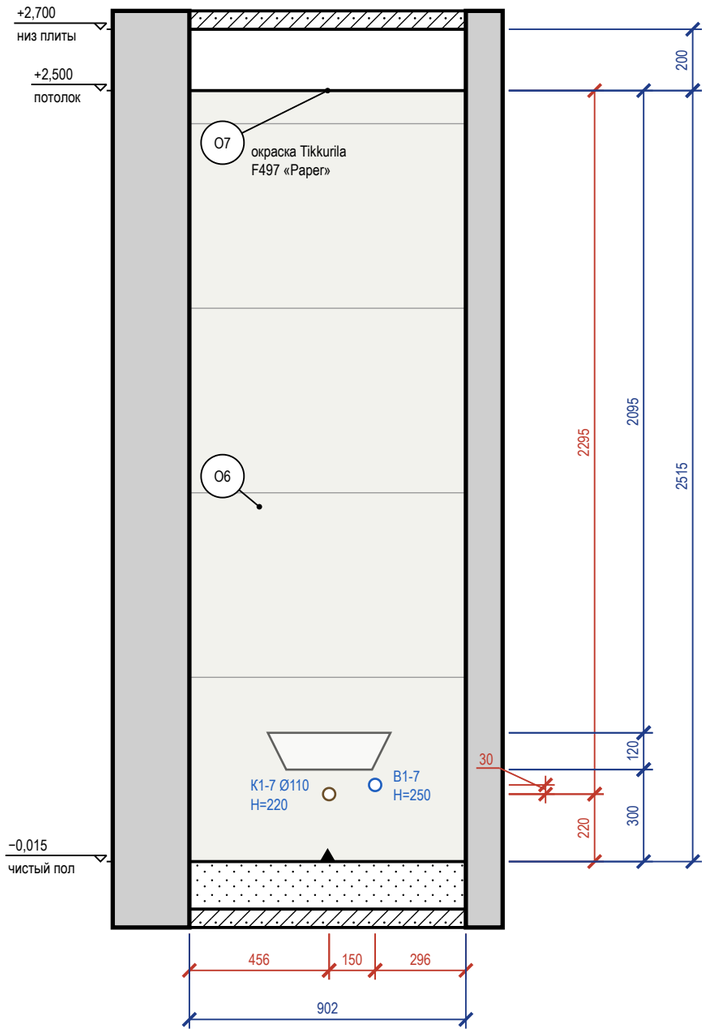


## Развёртка стены Г

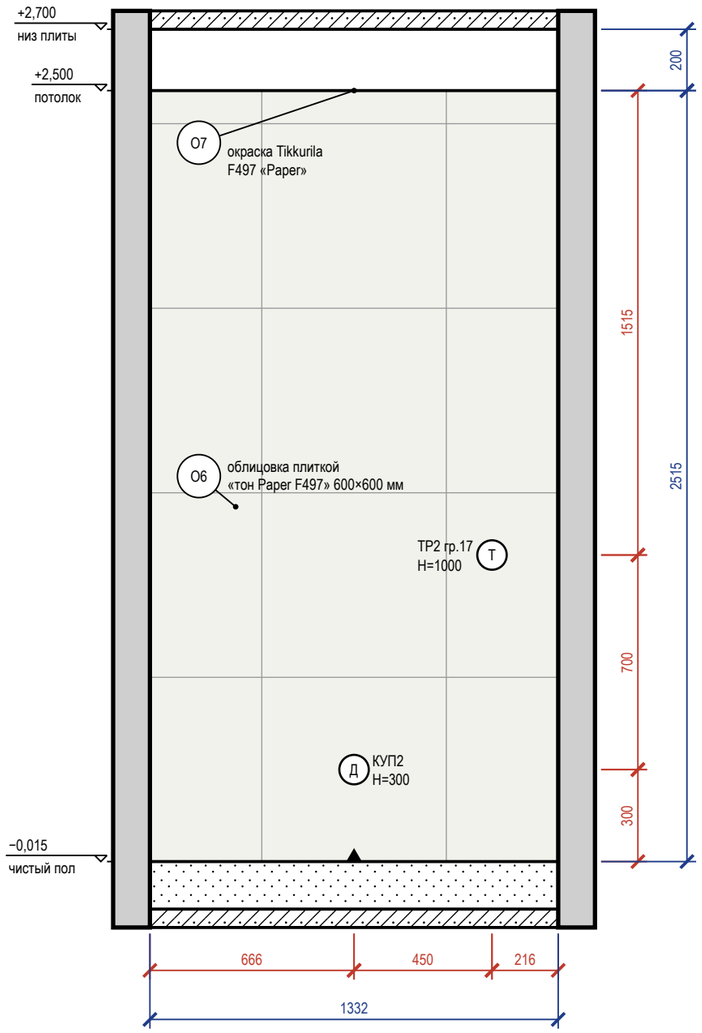


## Схема развёрток (М 1:100)




## Ведомость отделки (на листе)

| Марка | Поверхность | Материал, изделие | Цвет, код | Кол. |
|---|---|---|---|---|
| О6 | стены | облицовка плиткой, 600×600×9 мм, аналог: керамогранит матовый, тон F497, затирка CG2WA | #F1F1EC «тон Paper F497» | 5,6 м² |
| О7 | потолок | окраска, Tikkurila Luja 7, матовая, подготовка Q3 | Tikkurila F497 «Paper» | 1,3 м² |

Визуализация этой стены — лист 80



### Примечания

1. Размеры — в мм от чистовых поверхностей стен; условные обозначения и общие указания — лист 2.
2. Облицовка — по сетке швов 2 мм, раскладка от оси стены (треугольник у пола); подрезки — по листу раскладки плитки.
3. Гидроизоляция в 2 слоя, заход на стены 200 мм — до облицовки, с актом скрытых работ и тестом проливом (узел — на листе узлов).

| | Лист | № док. | Подпись | Дата |
|---|---|---|---|---|
| Дизайнер | Кырлан А.С. | | | 05.10.26 |

Проект: Четырёхкомнатная квартира

Развёртки стен В, Г. Санузел (пом. 10)

| Стадия | Лист | Листов |
|---|---|---|
| П | 82 | 111 |

выпуск 05.10.2026 № 05166c8858 · стр. 82 из 111



| | | | | | |
|---|---|---|---|---|---|
| | | | | | Проект: Четырёхкомнатная квартира |
| | Лист | № док. | Подпись | Дата | |
| Дизайнер | Кырлан А.С. | | | 05.10.26 | Визуализация гостиной |

| Стадия | Лист | Листов |
|---|---|---|
| П | 83 | 111 |

выпуск 05.10.2026 № 05166c8858 · стр. 83 из 111




| | | | | | |
|---|---|---|---|---|---|
| | | | | | Проект: Четырёхкомнатная квартира |
| | Лист | № док. | Подпись | Дата | |
| Дизайнер | Кырлан А.С. | | | 05.10.26 | Визуализация гостиной |


| Стадия | Лист | Листов |
|---|---|---|
| П | 84 | 111 |

выпуск 05.10.2026 № 05166c8858 · стр. 84 из 111

## Развёртка стены А

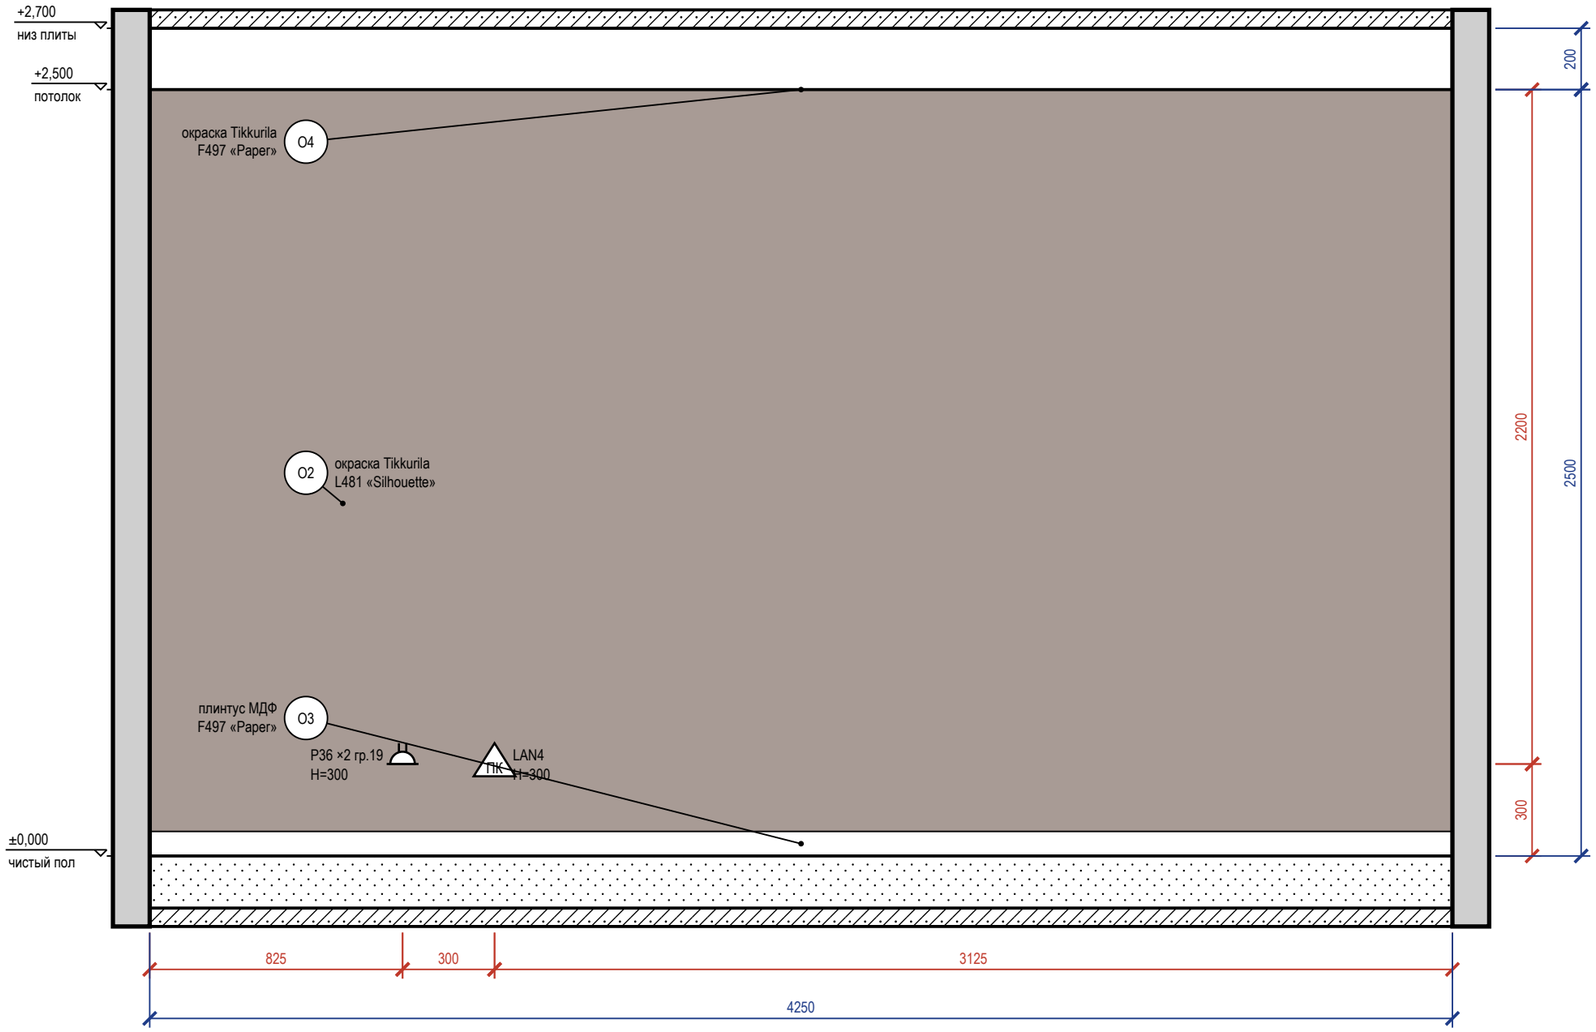


## Схема развёрток (М 1:100)

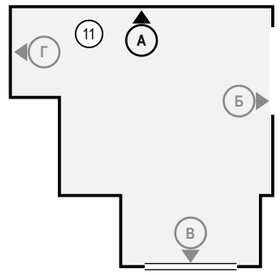


## Ведомость отделки (на листе)

| Марка | Поверхность | Материал, изделие | Цвет, код | Кол. |
|---|---|---|---|---|
| О2 | акцентная стена | окраска, Tikkurila Optiva 5 Matt, аналог: интерьерная краска, класс 2 по EN 13300, глубокоматовая/матовая, база С, матовая, подготовка К3 | Tikkurila L481 «Silhouette» | 10,6 м² |
| О3 | плинтус | плинтус МДФ, h 80 мм, аналог: плинтус МДФ под окраску 80×16 мм, полуглянцевая | Tikkurila F497 «Paper» | 4,3 м |
| О4 | потолок | окраска, Tikkurila Anti-Reflex 2, глубокоматовая, подготовка Q3 | Tikkurila F497 «Paper» | 14,6 м² |

Визуализация этой стены — лист 83



### Примечания

1. Размеры — в мм от чистовых поверхностей стен; условные обозначения и общие указания — лист 2.
2. Потолок на развёртках — по нижнему уровню У1; другие уровни потолка помещения: У2 +2,600.

| | Лист | № док. | Подпись | Дата |
|---|---|---|---|---|
| Дизайнер | Кырлан А.С. | | | 05.10.26 |


Проект: Четырёхкомнатная квартира

Развёртка стены А. Гостиная (пом. 11)


| Стадия | Лист | Листов |
|---|---|---|
| П | 85 | 111 |

выпуск 05.10.2026 № 05166c8858 · стр. 85 из 111

## Развёртка стены Б

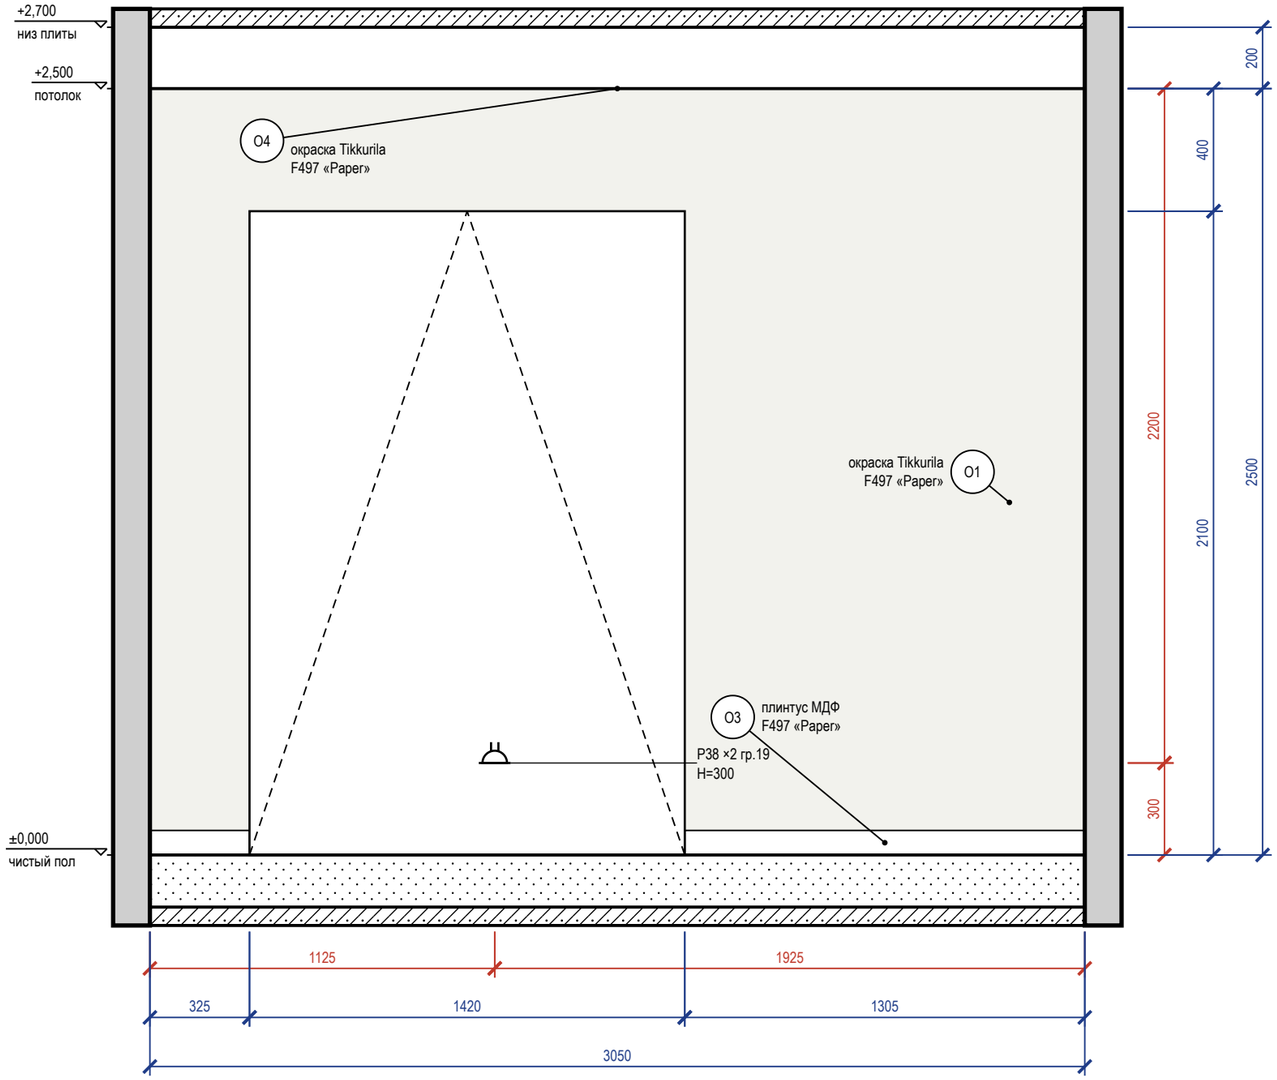


## Схема развёрток (М 1:100)

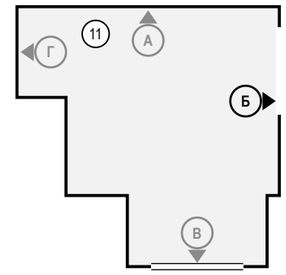


## Ведомость отделки (на листе)

| Марка | Поверхность | Материал, изделие | Цвет, код | Кол. |
|---|---|---|---|---|
| О1 | стены | окраска, Tikkurila Optiva 5 Matt, матовая, подготовка К3 | Tikkurila F497 «Paper» | 4,6 м² |
| О3 | плинтус | плинтус МДФ, h 80 мм, аналог: плинтус МДФ под окраску 80×16 мм, полуглянцевая | Tikkurila F497 «Paper» | 1,6 м |
| О4 | потолок | окраска, Tikkurila Anti-Reflex 2, глубокоматовая, подготовка Q3 | Tikkurila F497 «Paper» | 14,6 м² |

Визуализация этой стены — лист 84



### Примечания


1. Размеры — в мм от чистовых поверхностей стен; условные обозначения и общие указания — лист 2.
2. Потолок на развёртках — по нижнему уровню У1; другие уровни потолка помещения: У2 +2,600.

| | | | | | |
|---|---|---|---|---|---|
| | | | | | Проект: Четырёхкомнатная квартира |
| | Лист | № док. | Подпись | Дата | Развёртка стены Б. Гостиная (пом. 11) |
| Дизайнер | Кырлан А.С. | | | 05.10.26 | |


| Стадия | Лист | Листов |
|---|---|---|
| П | 86 | 111 |

выпуск 05.10.2026 № 05166c8858 · стр. 86 из 111


## Развёртка стены В

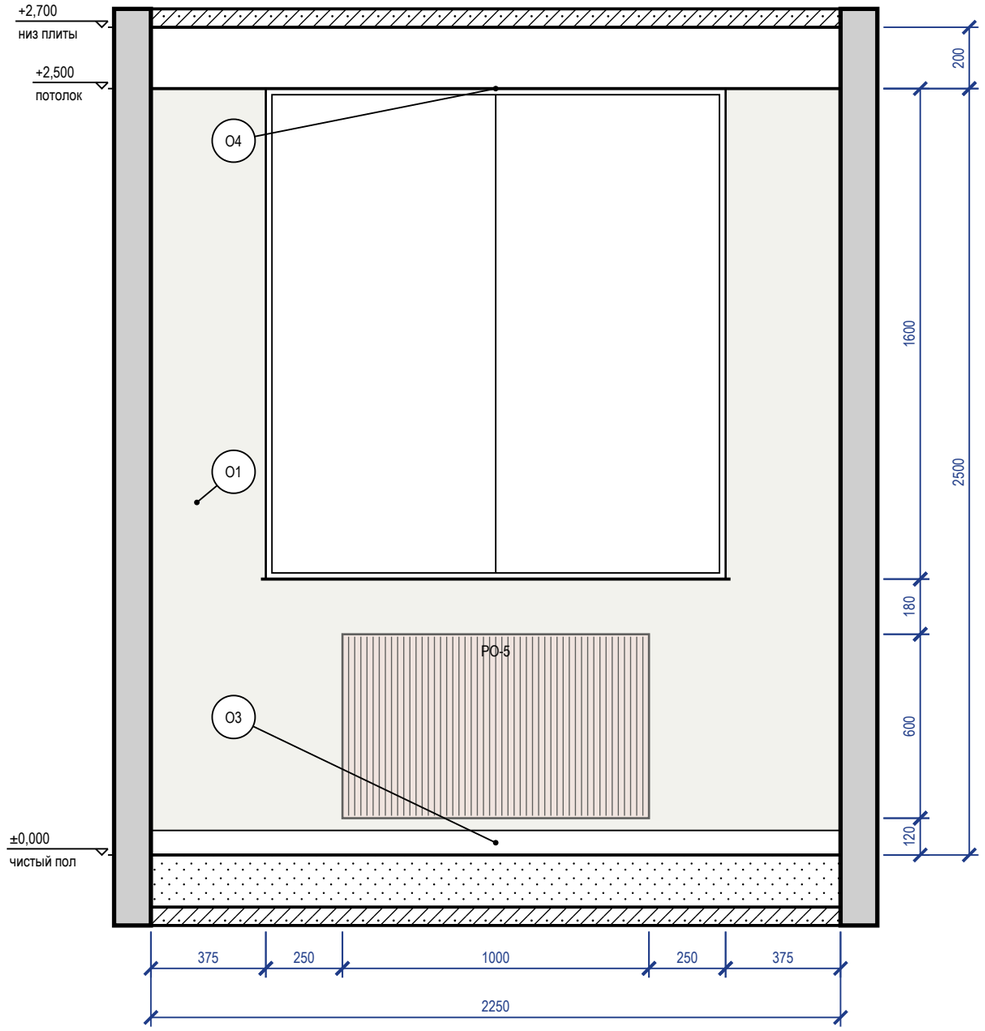


## Развёртка стены Г

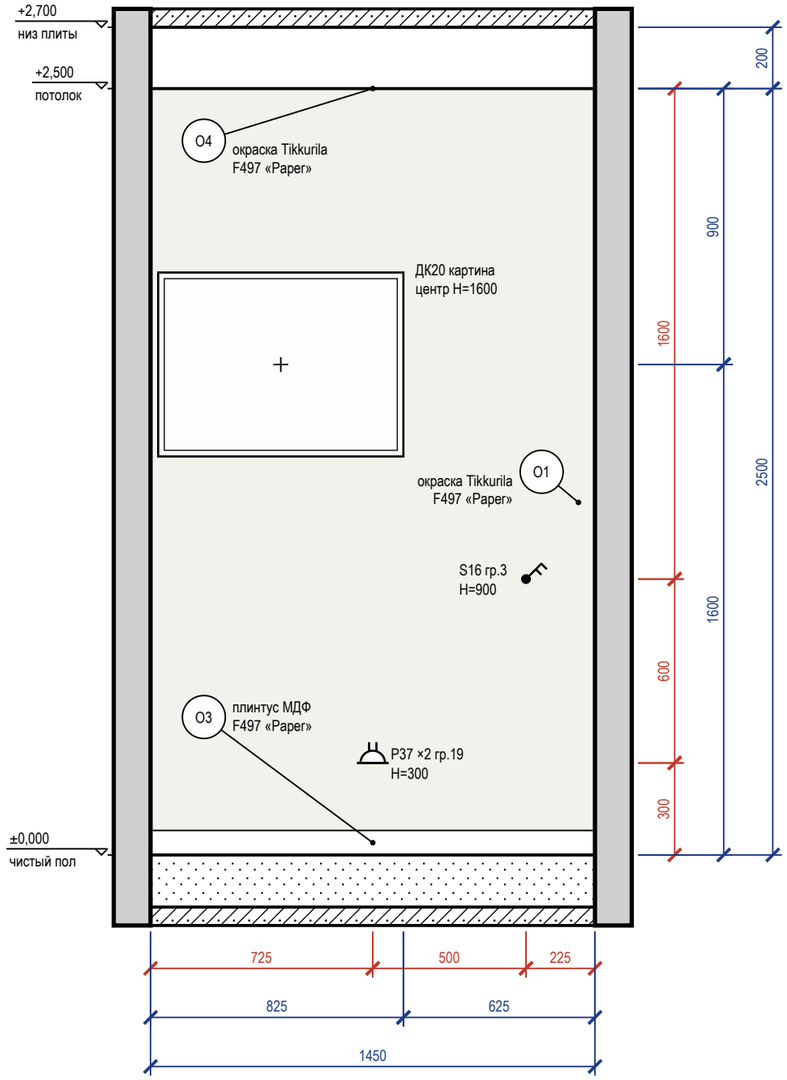


## Схема разверток (М 1:100)

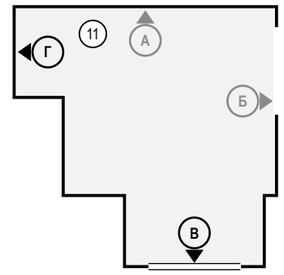


## Ведомость отделки (на листе)

| Марка | Поверхность | Материал, изделие | Цвет, код | Кол. |
|---|---|---|---|---|
| О1 | стены | окраска, Tikkurila Optiva 5 Matt, матовая, подготовка К3 | Tikkurila F497 «Paper» | 6,8 м² |
| О3 | плинтус | плинтус МДФ, h 80 мм, аналог: плинтус МДФ под окраску 80×16 мм, полуглянцевая | Tikkurila F497 «Paper» | 3,7 м |
| О4 | потолок | окраска, Tikkurila Anti-Reflex 2, глубокоматовая, подготовка Q3 | Tikkurila F497 «Paper» | 14,6 м² |

## Примечания

1. Размеры — в мм от чистовых поверхностей стен; условные обозначения и общие указания — лист 2.
2. Картины и зеркала крепить к основанию по паспорту изделия (закладные и анкеры — в перечне скрытых работ); крест — ось центра предмета.
3. Потолок на развёртках — по нижнему уровню У1; другие уровни потолка помещения: У2 +2,600.

| | | | | |
|---|---|---|---|---|
| | Лист | № док. | Подпись | Дата |
| Дизайнер | Кырлан А.С. | | | 05.10.26 |

Проект: Четырёхкомнатная квартира

Развёртки стен В, Г. Гостиная (пом. 11)

| Стадия | Лист | Листов |
|---|---|---|
| П | 87 | 111 |

выпуск 05.10.2026 № 05166c8858 · стр. 87 из 111




| | | | | | |
|---|---|---|---|---|---|
| | | | | | Проект: Четырёхкомнатная квартира |
| | Лист | № док. | Подпись | Дата | |
| Дизайнер | Кырлан А.С. | | | 05.10.26 | Визуализация: Гардеробная 1 |


| Стадия | Лист | Листов |
|---|---|---|
| П | 88 | 111 |

выпуск 05.10.2026 № 05166c8858 · стр. 88 из 111

## Развёртка стены А

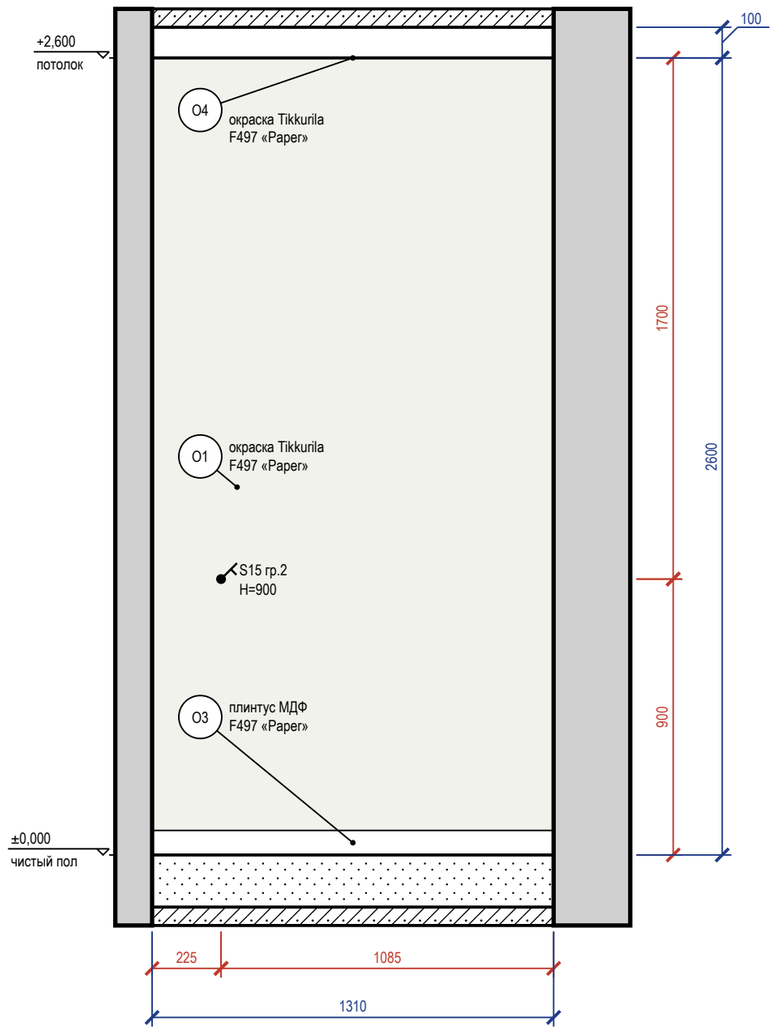



## Развёртка стены Б

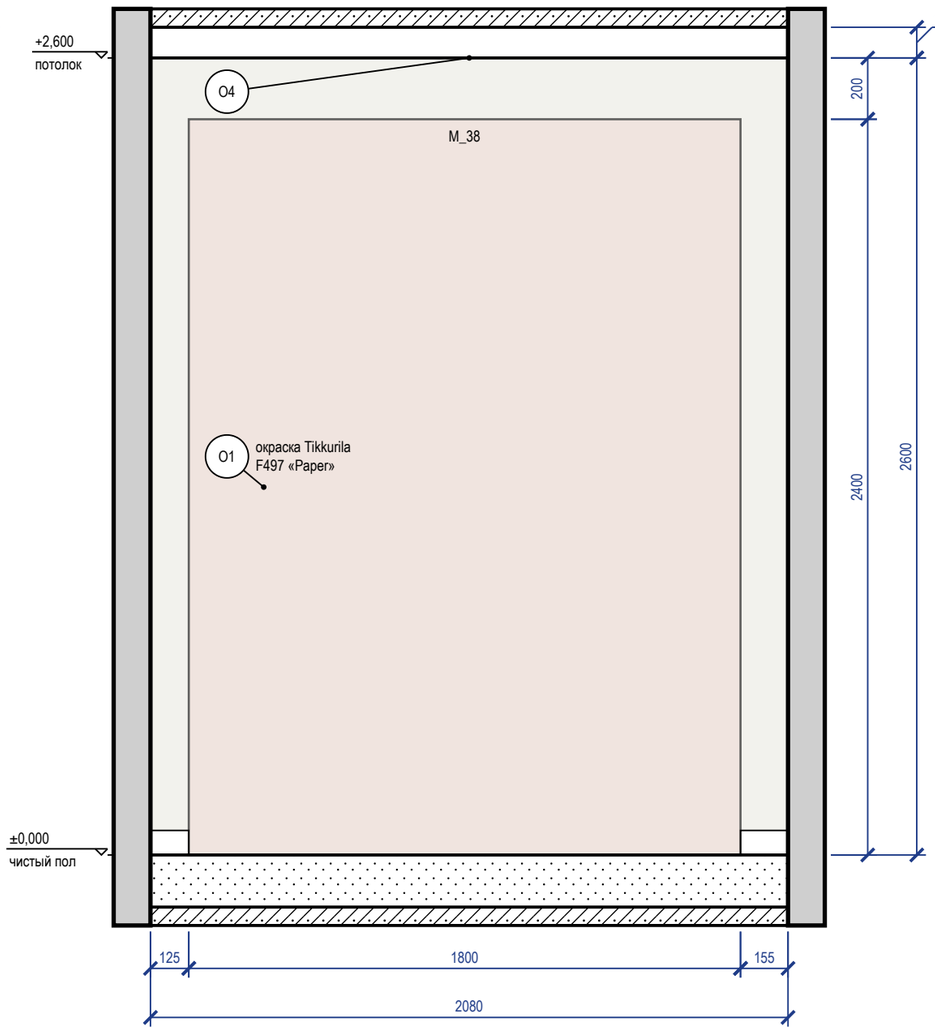


Визуализация этой стены — лист 88



### Схема развёрток (М 1:100)

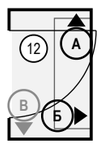


### Ведомость отделки (на листе)

| Марка | Поверхность | Материал, изделие | Цвет, код | Кол. |
|---|---|---|---|---|
| О1 | стены | окраска, Tikkurila Optiva 5 Matt, матовая, подготовка К3 | Tikkurila F497 «Paperг» | 8,8 м² |
| О3 | плинтус | плинтус МДФ, h 80 мм, аналог: плинтус МДФ под окраску 80×16 мм, полуглянцевая | Tikkurila F497 «Paperг» | 1,6 м |
| О4 | потолок | окраска, Tikkurila Anti-Reflex 2, глубокоматовая, подготовка Q3 | Tikkurila F497 «Paperг» | 2,8 м² |

### Примечания


1. Размеры — в мм от чистовых поверхностей стен; условные обозначения и общие указания — лист 2.

| | | | | | |
|---|---|---|---|---|---|
| | | | | | Проект: Четырёхкомнатная квартира |
| | Лист | № док. | Подпись | Дата | Развёртки стен А, Б. Гардеробная 1 (пом. 12) |
| Дизайнер | Кырлан А.С. | | | 05.10.26 | |


| Стадия | Лист | Листов |
|---|---|---|
| П | 89 | 111 |

выпуск 05.10.2026 № 05166c8858 · стр. 89 из 111

## Развёртка стены В

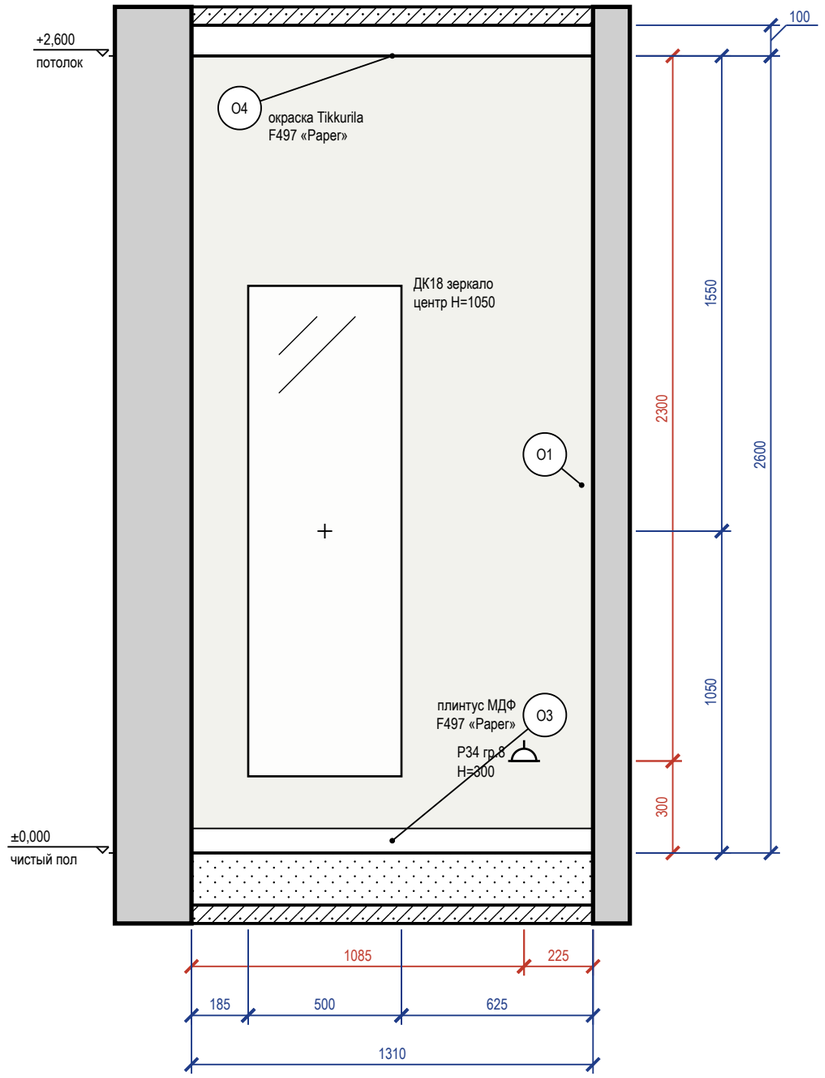


## Схема развёрток (М 1:100)

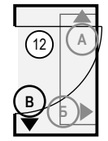


## Ведомость отделки (на листе)

| Марка | Поверхность | Материал, изделие | Цвет, код | Кол. |
|---|---|---|---|---|
| О1 | стены | окраска, Tikkurila Optiva 5 Matt, матовая, подготовка К3 | Tikkurila F497 «Paper» | 3,4 м² |
| О3 | плинтус | плинтус МДФ, h 80 мм, аналог: плинтус МДФ под окраску 80×16 мм, полуглянцевая | Tikkurila F497 «Paper» | 1,3 м |
| О4 | потолок | окраска, Tikkurila Anti-Reflex 2, глубокоматовая, подготовка Q3 | Tikkurila F497 «Paper» | 2,8 м² |

## Примечания

1. Размеры — в мм от чистовых поверхностей стен; условные обозначения и общие указания — лист 2.
2. Картины и зеркала крепить к основанию по паспорту изделия (закладные и анкеры — в перечне скрытых работ); крест — ось центра предмета.

| | | | | | |
|---|---|---|---|---|---|
| | | | | | Проект: Четырёхкомнатная квартира |
| | Лист | № док. | Подпись | Дата | Развёртка стены В. Гардеробная 1 (пом. 12) |
| Дизайнер | Кырлан А.С. | | | 05.10.26 | |

| Стадия | Лист | Листов |
|---|---|---|
| П | 90 | 111 |

выпуск 05.10.2026 № 05166c8858 · стр. 90 из 111




| | | | | | |
|---|---|---|---|---|---|
| | | | | | Проект: Четырёхкомнатная квартира |
| | | | | | |
| | Лист | № док. | Подпись | Дата | |
| Дизайнер | Кырлан А.С. | | | 05.10.26 | Визуализация: Балкон 1 |
| | | | | | |


| Стадия | Лист | Листов |
|---|---|---|
| П | 91 | 111 |

выпуск 05.10.2026 № 05166c8858 · стр. 91 из 111


## Развёртка стены А

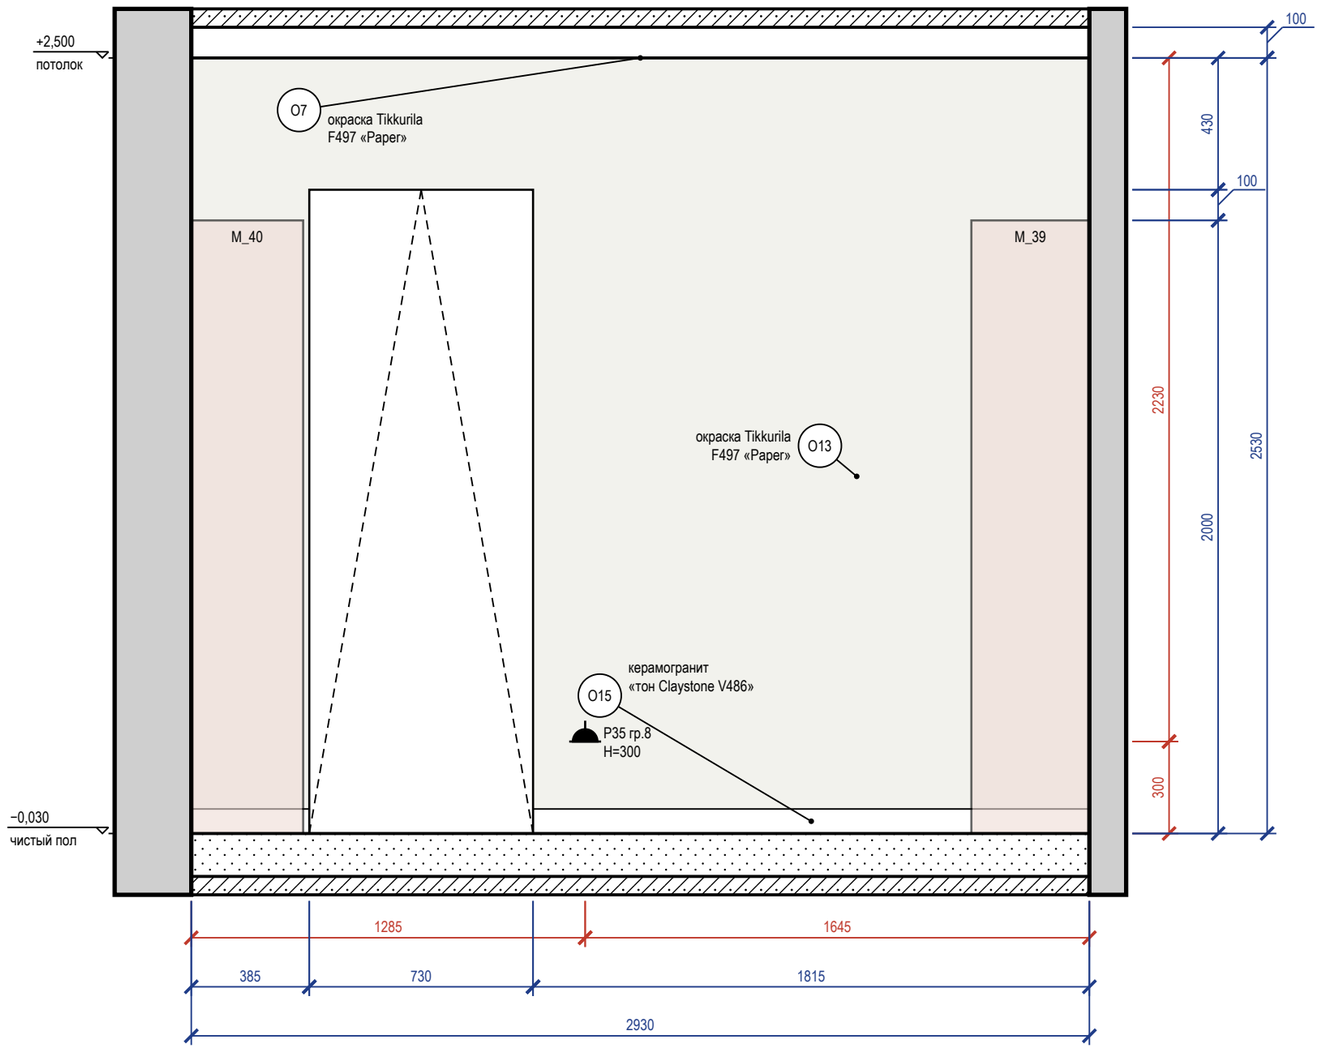


## Развёртка стены Б

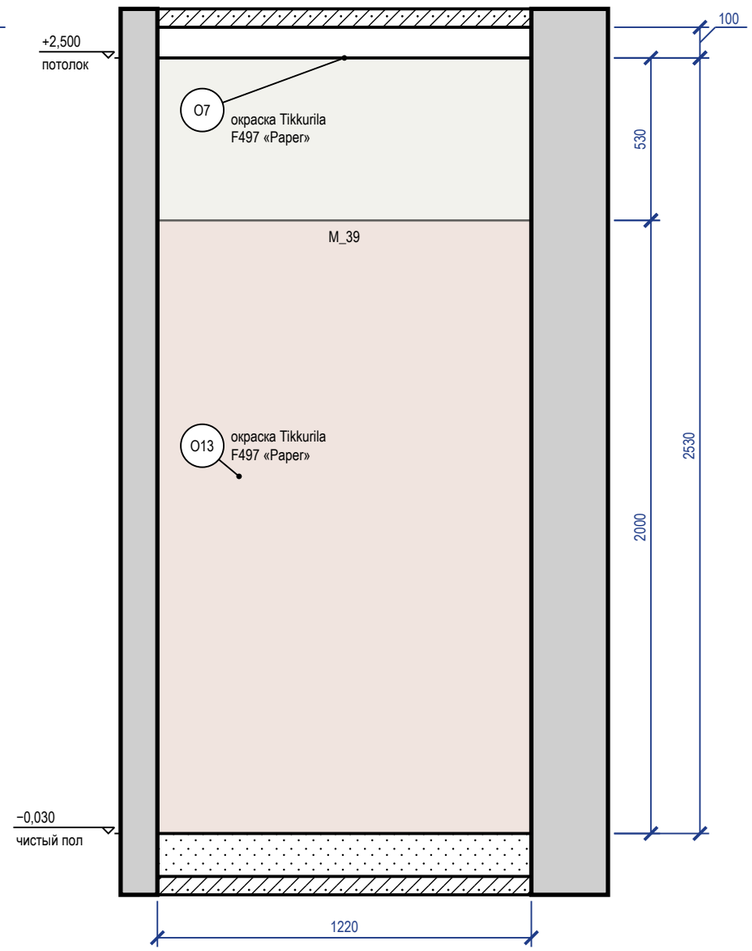


### Схема развёрток (М 1:100)

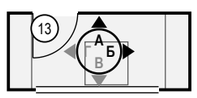


### Ведомость отделки (на листе)

| Марка | Поверхность | Материал, изделие | Цвет, код | Кол. |
|---|---|---|---|---|
| О7 | потолок | окраска, Tikkurila Luja 7, матовая, подготовка Q3 | Tikkurila F497 «Paper» | 3,7 м² |
| О13 | стены | окраска, Tikkurila Luja 7, шелковисто-матовая, подготовка К3 | Tikkurila F497 «Paper» | 9 м² |
| О15 | плинтус | керамогранит, аналог: плинтус из керамогранита пола, подрезка 80 мм, верхняя кромка с запилом 45° | #B8AFA5 «тон Claystone V486» | 2,2 м |

### Примечания


1. Размеры — в мм от чистовых поверхностей стен; условные обозначения и общие указания — лист 2.

| | | | | | |
|---|---|---|---|---|---|
| | | | | | Проект: Четырёхкомнатная квартира |
| | Лист | № док. | Подпись | Дата | Развёртки стен А, Б. Балкон 1 (пом. 13) |
| Дизайнер | Кырлан А.С. | | | 05.10.26 | |


| Стадия | Лист | Листов |
|---|---|---|
| П | 92 | 111 |

выпуск 05.10.2026 № 05166c8858 · стр. 92 из 111


## Развёртка стены В

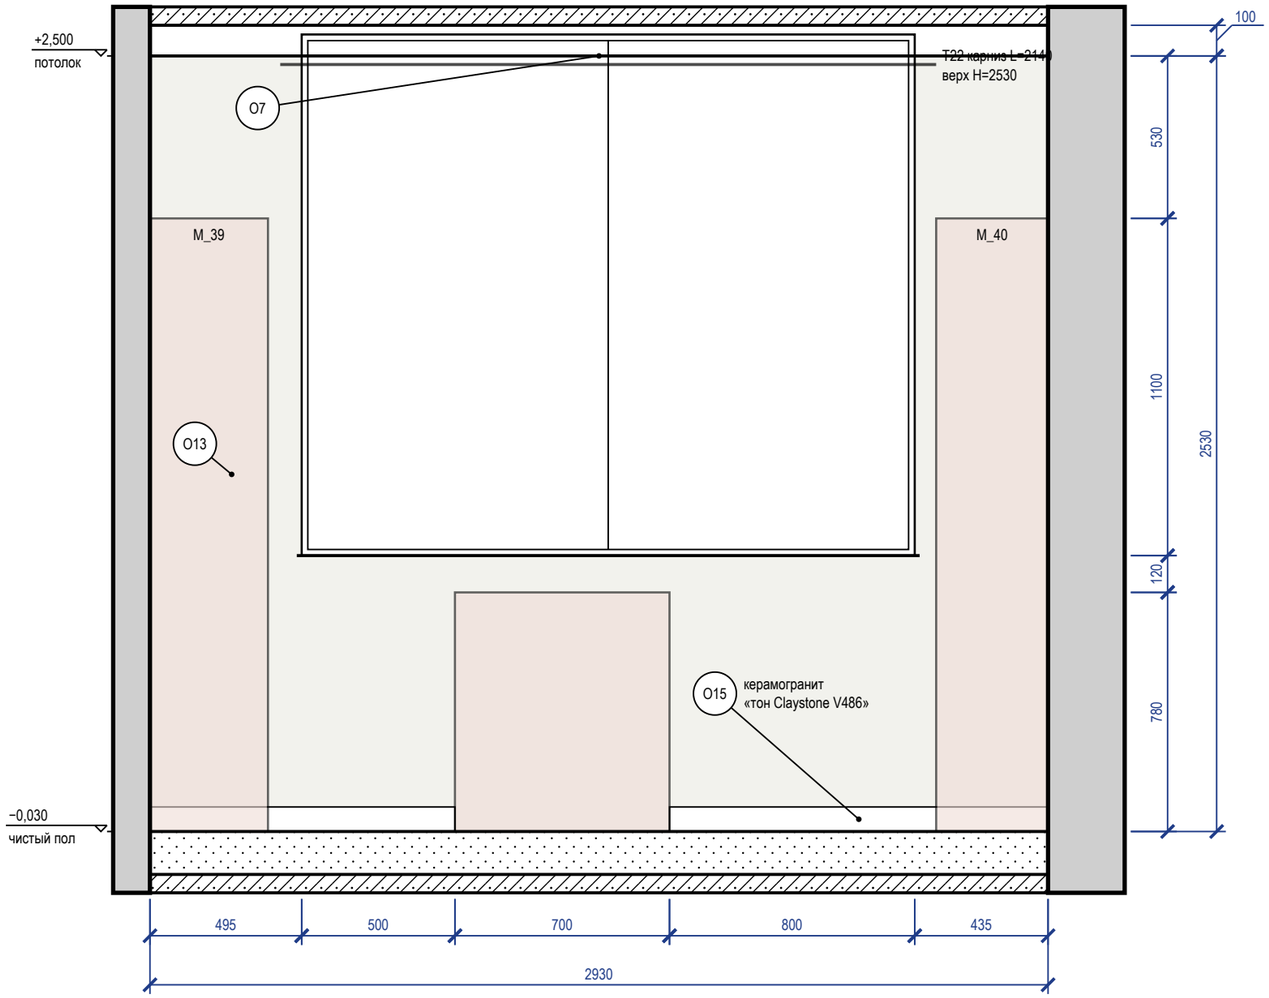


## Развёртка стены Г

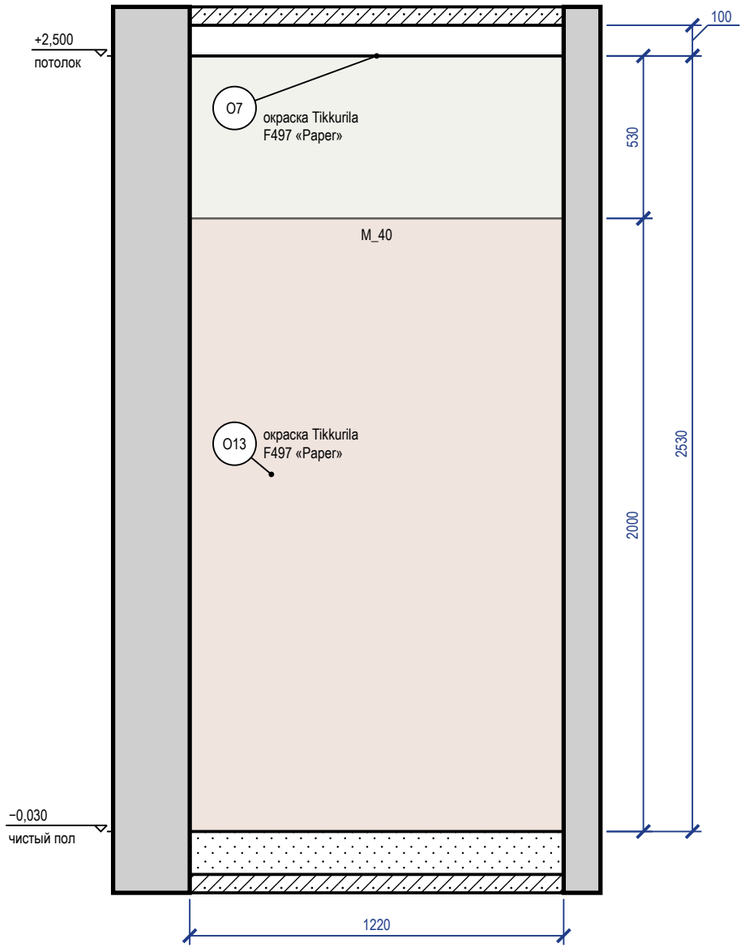


### Схема развёрток (М 1:100)

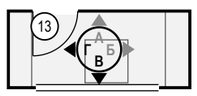


### Ведомость отделки (на листе)

| Марка | Поверхность | Материал, изделие | Цвет, код | Кол. |
|---|---|---|---|---|
| О7 | потолок | окраска, Tikkurila Luja 7, матовая, подготовка Q3 | Tikkurila F497 «Paper» | 3,7 м² |
| О13 | стены | окраска, Tikkurila Luja 7, шелковисто-матовая, подготовка К3 | Tikkurila F497 «Paper» | 7,2 м² |
| О15 | плинтус | керамогранит, аналог: плинтус из керамогранита пола, подрезка 80 мм, верхняя кромка с запилом 45° | #B8AFA5 «тон Claystone V486» | 2,2 м |

Визуализация этой стены — лист 91



### Примечания


1. Размеры — в мм от чистовых поверхностей стен; условные обозначения и общие указания — лист 2.
2. Карнизы (шины) — по ведомости текстиля декоратора; длина L и верх H — по развёртке, крепление — до окраски потолка.

| | | | | | |
|---|---|---|---|---|---|
| | | | | | Проект: Четырёхкомнатная квартира |
| | Лист | № док. | Подпись | Дата | Развёртки стен В, Г. Балкон 1 (пом. 13) |
| Дизайнер | Кырлан А.С. | | | 05.10.26 | |


| Стадия | Лист | Листов |
|---|---|---|
| П | 93 | 111 |

выпуск 05.10.2026 № 05166c8858 · стр. 93 из 111


**Общий вид**

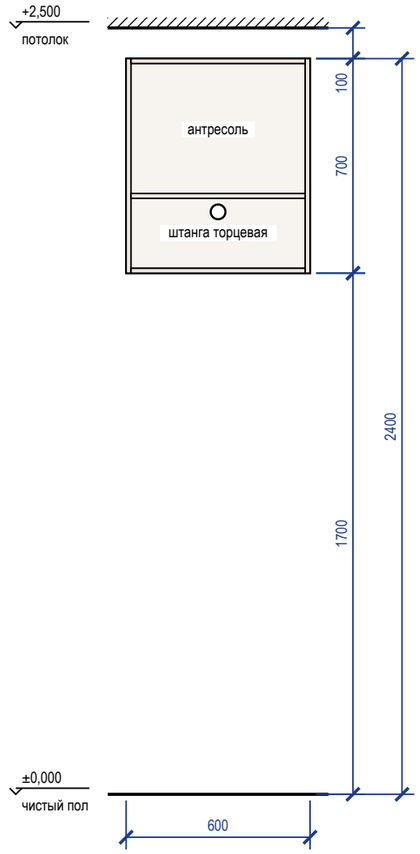


**Наполнение, размеры в свету**

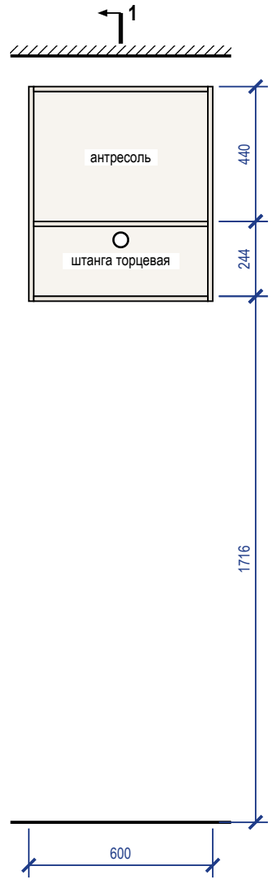



**Разрез 1-1**

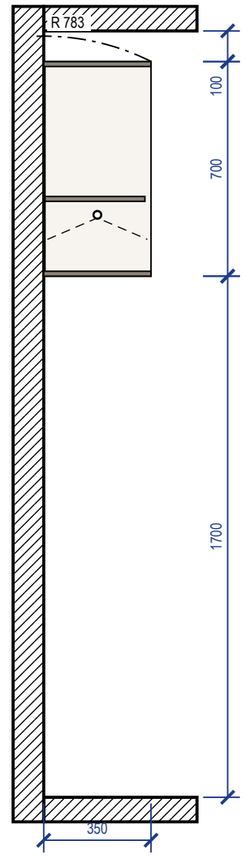


## Примечания

1. Размеры — в мм по чистовой отделке; изделие 600×350×700 (Ш×Г×В). Перед раскроем — контрольный замер цеха после чистовой отделки стен, пола и потолка.
2. Корпус — ЛДСП 16 мм, задняя стенка ХДФ 4 мм в паз, цоколь 0 мм на регулируемых опорах; открытая система без фасадов, ящики с фасадами.
3. Кромка: скрытые торцы 0,4 мм, видимые 2 мм (ПВХ/АБС).
4. Номинальные зазоры: между фасадами ящиков 3 мм, фасад ящика — стойка 2 мм.
5. Ящики — направляющие полного выдвижения NL 300 (внутренняя глубина 346 мм ≥ NL + 3); присадка по 32-й системе — выполняет цех.
6. Зазор до потолка 100 мм — закрыть планкой в цвет корпуса при монтаже.
7. Подъём корпуса: диагональ боковины $\sqrt{(700^2 + 350^2)} = 783$ мм < 800 мм до потолка — корпус собирается лёжа и поднимается поворотом.
8. Крепление к стене от опрокидывания: крепление к стене, 2 точки; основание стены и шаг анкеров — монтажная схема шкафов.

**3D орто**

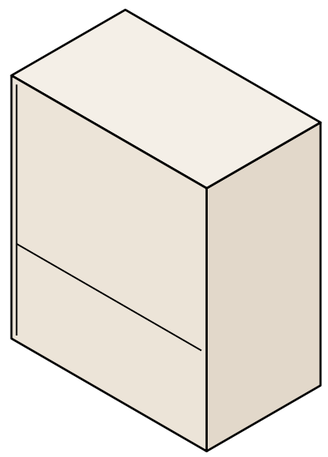


| | | | | | |
|---|---|---|---|---|---|
| | | | | | Проект: Четырёхкомнатная квартира |
| | Лист | № док. | Подпись | Дата | |
| Дизайнер | Кырлан А.С. | | | 05.10.26 | Система хранения M_07 |


| Стадия | Лист | Листов |
|---|---|---|
| П | Д_1 | 111 |

выпуск 05.10.2026 № 05166c8858 · стр. 94 из 111


## Общий вид

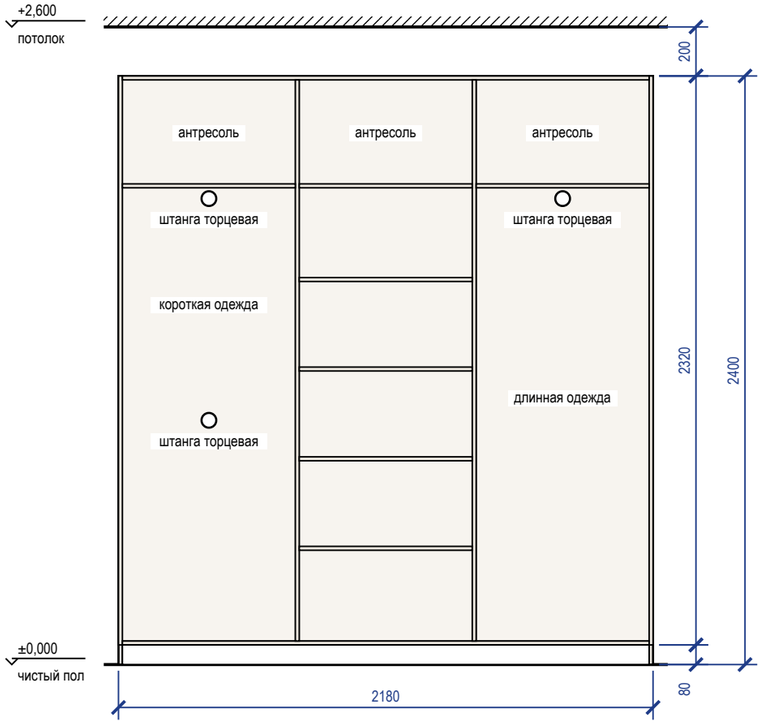



## Наполнение, размеры в свету

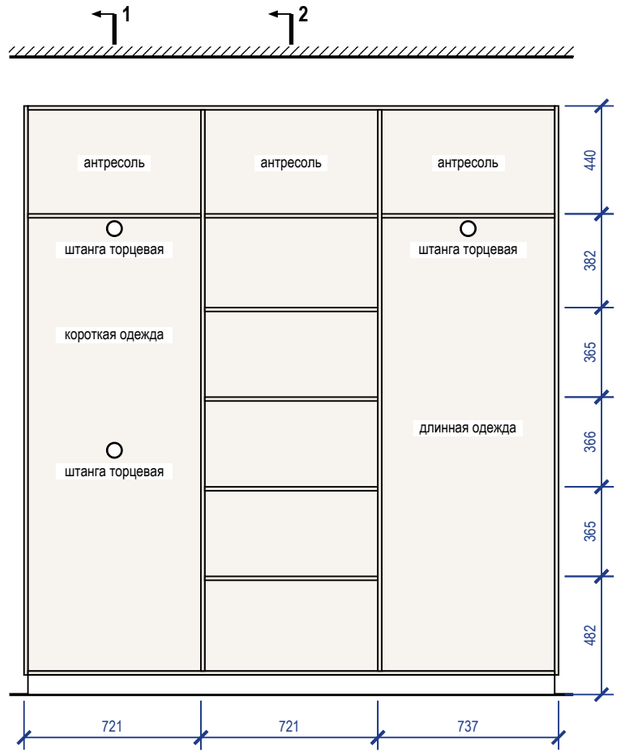


## Разрез 1-1

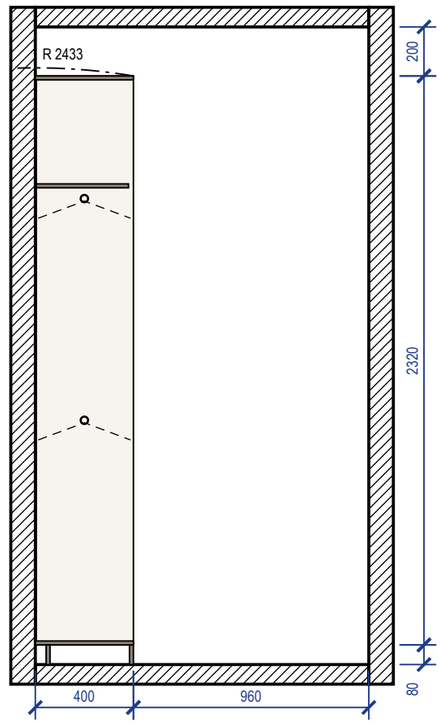



## Разрез 2-2

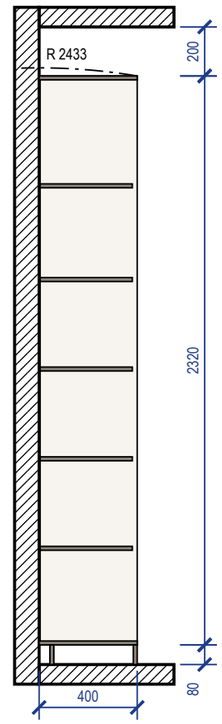


### Примечания

1. Размеры — в мм по чистовой отделке; изделие 2180×400×2400 (Ш×Г×В). Перед раскроем — контрольный замер цеха после чистовой отделки стен, пола и потолка.
2. Корпус — ЛДСП 16 мм, задняя стенка ХДФ 4 мм в паз, цоколь 80 мм на регулируемых опорах; открытая система без фасадов, ящики с фасадами.
3. Кромка: скрытые торцы 0,4 мм, видимые 2 мм (ПВХ/АБС).
4. Номинальные зазоры: между фасадами ящиков 3 мм, фасад ящика — стойка 2 мм.
5. Ящики — направляющие полного выдвижения NL 350 (внутренняя глубина 396 мм ≥ NL + 3); присадка по 32-й системе — выполняет цех.
6. Зазор до потолка 200 мм.
7. Подъём корпуса: диагональ боковины $\sqrt{(2400^2 + 400^2)} = 2433$ мм < 2600 мм до потолка — корпус собирается лёжа и поднимается поворотом.
8. Крепление к стене от опрокидывания: крепление к стене, 4 точки; основание стены и шаг анкеров — монтажная схема шкафов.
9. Проход перед изделием 960 мм показан на разрезе 1-1.

## 3D орто

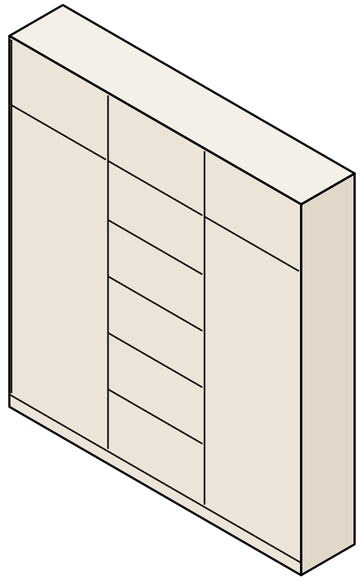


| | | | | | |
|---|---|---|---|---|---|
| | | | | | Проект: Четырёхкомнатная квартира |
| | Лист | № док. | Подпись | Дата | |
| Дизайнер | Кырлан А.С. | | | 05.10.26 | Система хранения М_08 |


| Стадия | Лист | Листов |
|---|---|---|
| П | Д_2 | 111 |

выпуск 05.10.2026 № 0516c8858 · стр. 95 из 111


**Общий вид**

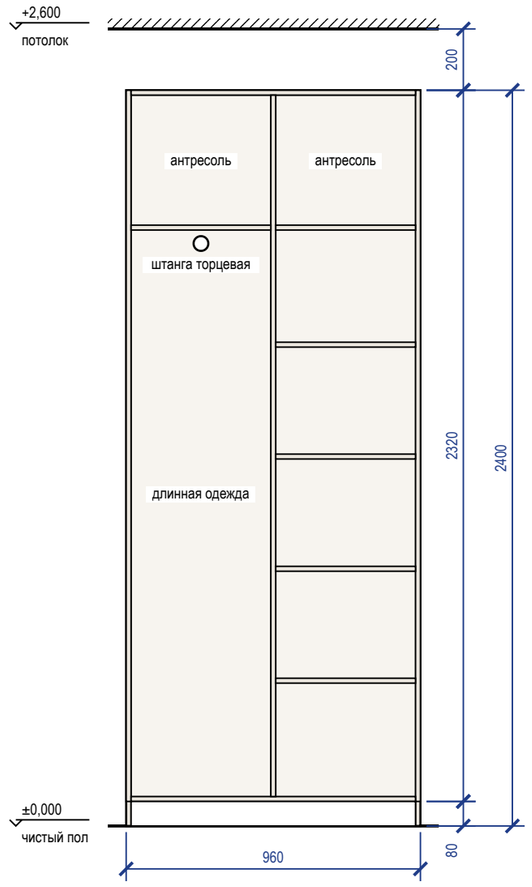



**Наполнение, размеры в свету**

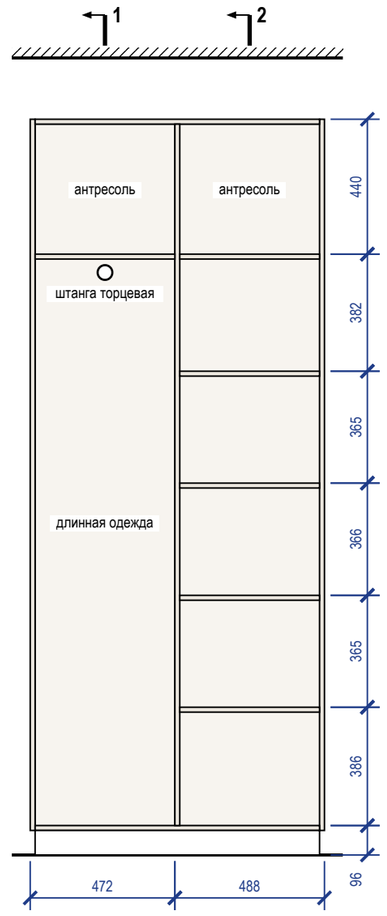


**Разрез 1-1**

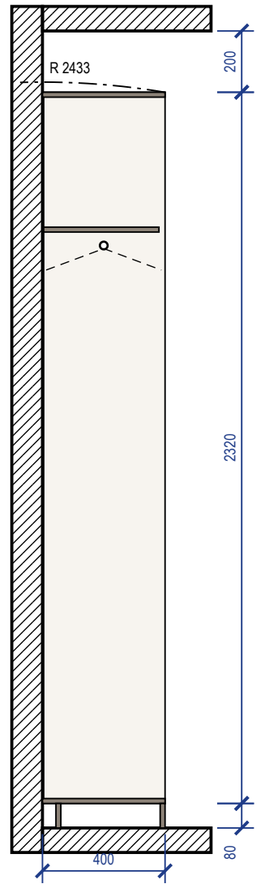



**Разрез 2-2**

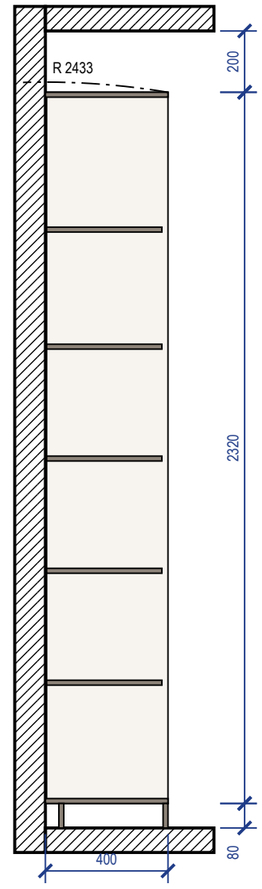


## Примечания

1. Размеры — в мм по чистовой отделке; изделие 960×400×2400 (Ш×Г×В). Перед раскроем — контрольный замер цеха после чистовой отделки стен, пола и потолка.
2. Корпус — ЛДСП 16 мм, задняя стенка ХДФ 4 мм в паз, цоколь 80 мм на регулируемых опорах; открытая система без фасадов, ящики с фасадами.
3. Кромка: скрытые торцы 0,4 мм, видимые 2 мм (ПВХ/АБС).
4. Номинальные зазоры: между фасадами ящиков 3 мм, фасад ящика — стойка 2 мм.
5. Ящики — направляющие полного выдвижения NL 350 (внутренняя глубина 396 мм ≥ NL + 3); присадка по 32-й системе — выполняет цех.
6. Зазор до потолка 200 мм.
7. Подъём корпуса: диагональ боковины $\sqrt{(2400^2 + 400^2)} = 2433$ мм < 2600 мм до потолка — корпус собирается лёжа и поднимается поворотом.
8. Крепление к стене от опрокидывания: крепление к стене, 3 точки; основание стены и шаг анкеров — монтажная схема шкафов.


**3D орто**

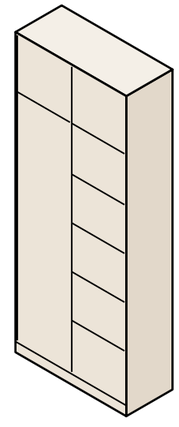


| | | | | | | | |
|---|---|---|---|---|---|---|---|
| | | | | | Проект: Четырёхкомнатная квартира | | |
| | Лист | № док. | Подпись | Дата | | | |
| Дизайнер | Кырлан А.С. | | | 05.10.26 | Система хранения М_09 | Стадия | Лист | Листов |
| | | | | | | П | Д_3 | 111 |

выпуск 05.10.2026 № 05166c8858 · стр. 96 из 111


**Вид с фасадами**

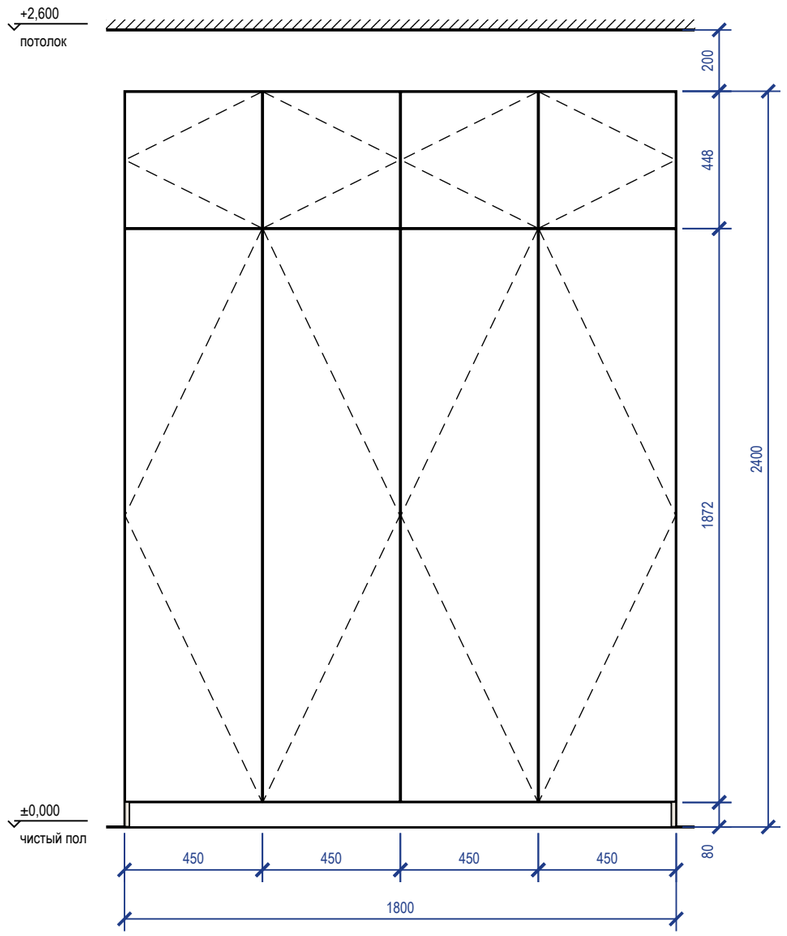



**Вид без фасадов**

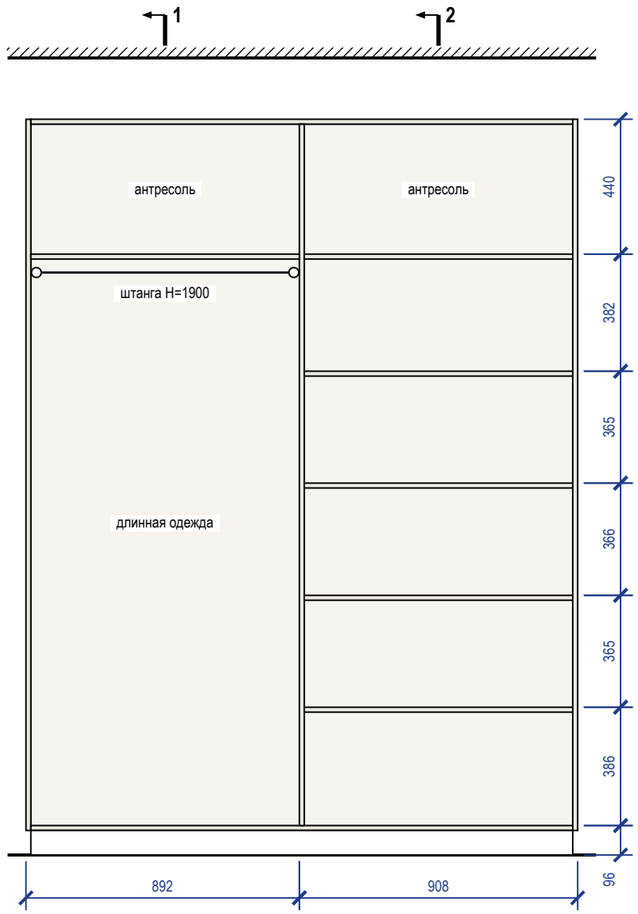


**Разрез 1-1**

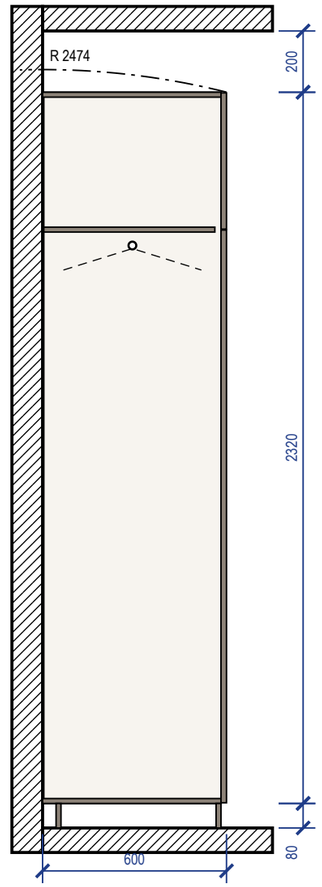



**Разрез 2-2**

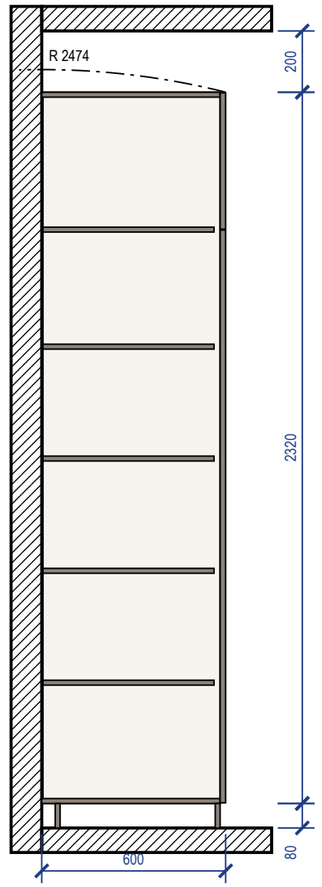


## Примечания

1. Размеры — в мм по чистовой отделке; изделие 1800×600×2400 (Ш×Г×В). Перед раскроем — контрольный замер цеха после чистовой отделки стен, пола и потолка.
2. Корпус — ЛДСП 16 мм, задняя стенка ХДФ 4 мм в паз, цоколь 80 мм на регулируемых опорах; фасады — МДФ, эмаль матовая 18 мм накладные, цвет — по колерной карте; петли с доводчиком: фасад 1869 мм — 4 петли, фасад 445 мм — 2 петли.
3. Кромка: скрытые торцы 0,4 мм, видимые 2 мм (ПВХ/АБС).
4. Номинальные зазоры: между фасадами 3 мм, фасад — стена и фасад — потолок не менее 3 мм, фасад ящика — стойка 2 мм.
5. Ящики — направляющие полного выдвижения NL 550 (внутренняя глубина 578 мм ≥ NL + 3); присадка по 32-й системе — выполняет цех.
6. Зазор до потолка 200 мм.
7. Подъём корпуса: диагональ боковины $\sqrt{(2400^2 + 600^2)}$ = 2474 мм < 2600 мм до потолка — корпус собирается лёжа и поднимается поворотом.
8. Крепление к стене от опрокидывания: уголок к стене, 3 шт.; основание стены и шаг анкеров — монтажная схема шкафов.


**3D орто**

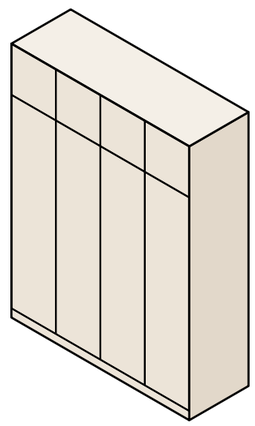


| | | | | | | | |
|---|---|---|---|---|---|---|---|
| | | | | | Проект: Четырёхкомнатная квартира | | |
| | Лист | № док. | Подпись | Дата | | | |
| Дизайнер | Кырлан А.С. | | | 05.10.26 | Шкаф распашной М_15 | Стадия | Лист | Листов |
| | | | | | | П | Д_4 | 111 |

выпуск 05.10.2026 № 05166c8858 · стр. 97 из 111


## Общий вид

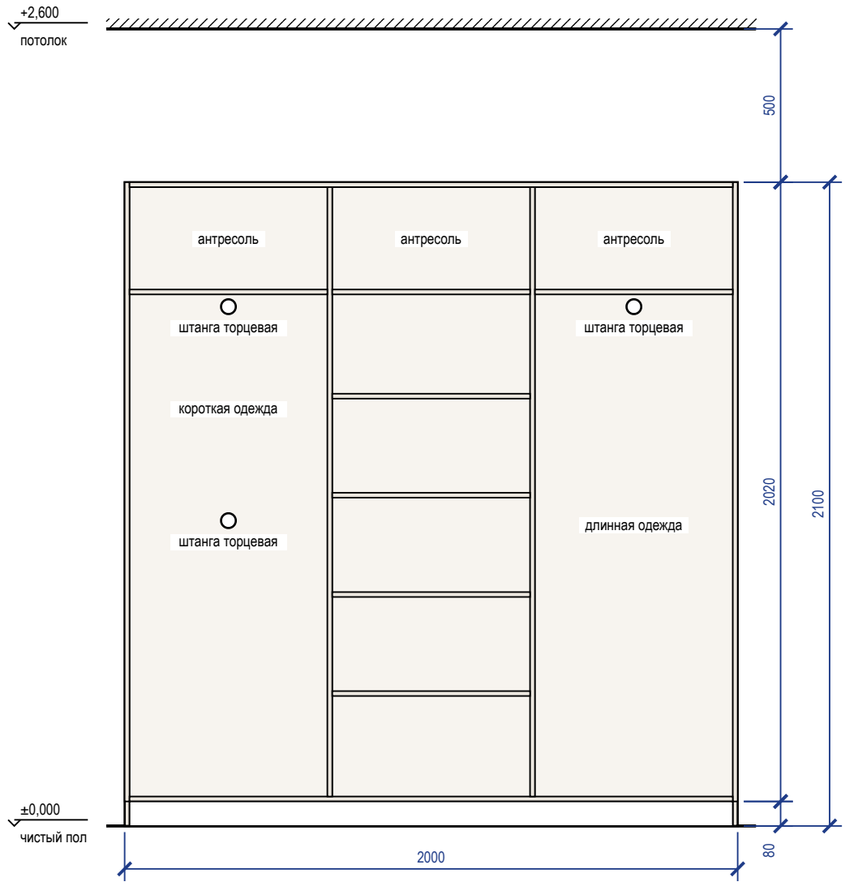



## Наполнение, размеры в свету

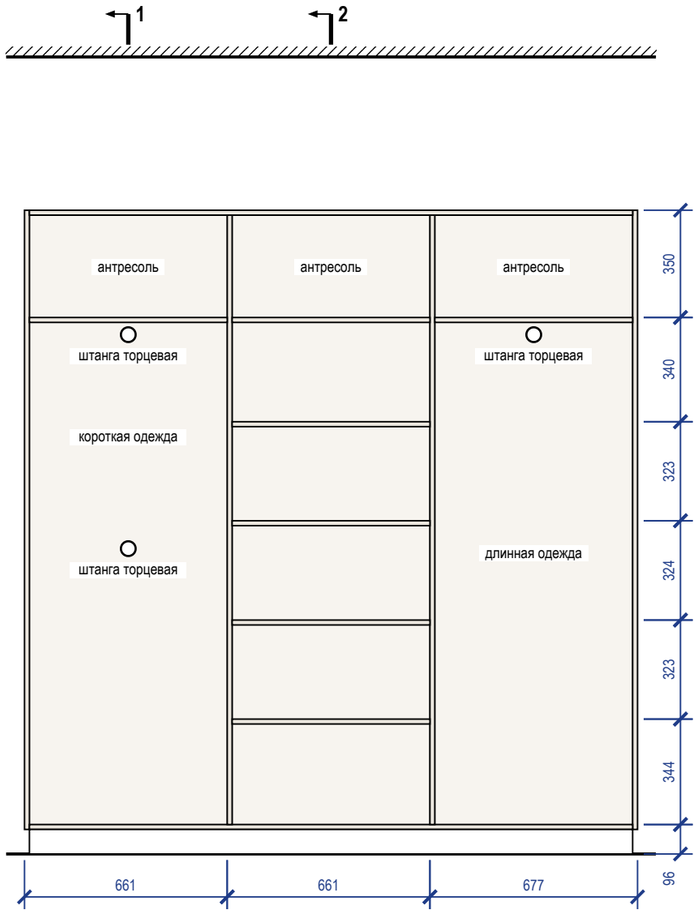


## Разрез 1-1

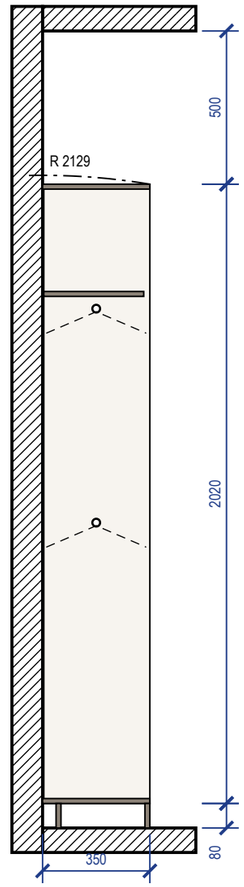



## Разрез 2-2

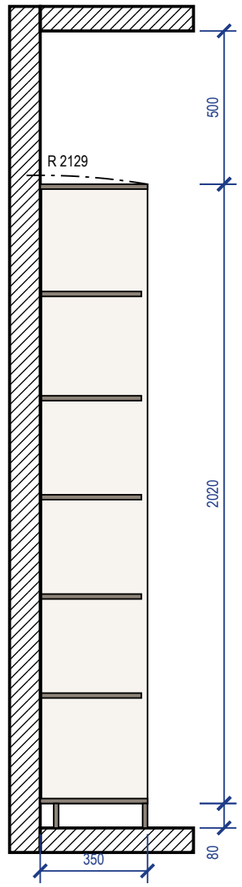


### Примечания

1. Размеры — в мм по чистовой отделке; изделие 2000×350×2100 (Ш×Г×В). Перед раскроем — контрольный замер цеха после чистовой отделки стен, пола и потолка.
2. Корпус — ЛДСП 16 мм, задняя стенка ХДФ 4 мм в паз, цоколь 80 мм на регулируемых опорах; открытая система без фасадов, ящики с фасадами.
3. Кромка: скрытые торцы 0,4 мм, видимые 2 мм (ПВХ/АБС).
4. Номинальные зазоры: между фасадами ящиков 3 мм, фасад ящика — стойка 2 мм.
5. Ящики — направляющие полного выдвижения NL 300 (внутренняя глубина 346 мм ≥ NL + 3); присадка по 32-й системе — выполняет цех.
6. Зазор до потолка 500 мм.
7. Подъём корпуса: диагональ боковины $\sqrt{(2100^2 + 350^2)} = 2129$ мм < 2600 мм до потолка — корпус собирается лёжа и поднимается поворотом.
8. Крепление к стене от опрокидывания: крепление к стене, 3 точки; основание стены и шаг анкеров — монтажная схема шкафов.

## 3D орто

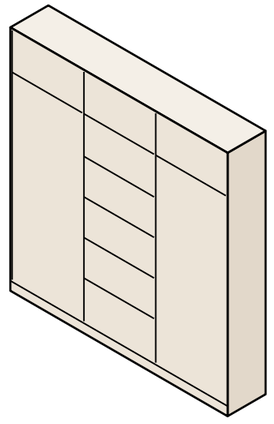


| | | | | | |
|---|---|---|---|---|---|
| | | | | | Проект: Четырёхкомнатная квартира |
| | Лист | № док. | Подпись | Дата | |
| Дизайнер | Кырлан А.С. | | | 05.10.26 | Система хранения M_17 |


| Стадия | Лист | Листов |
|---|---|---|
| П | Д_5 | 111 |

выпуск 05.10.2026 № 0516c8858 · стр. 98 из 111


## Вид с фасадами

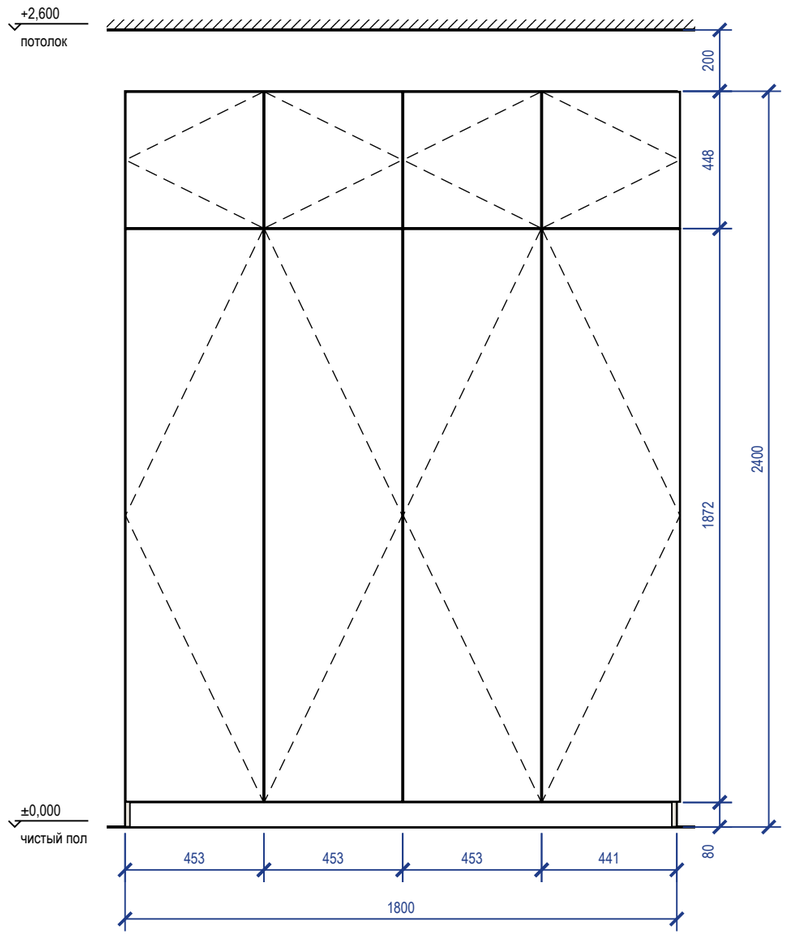


## Вид без фасадов

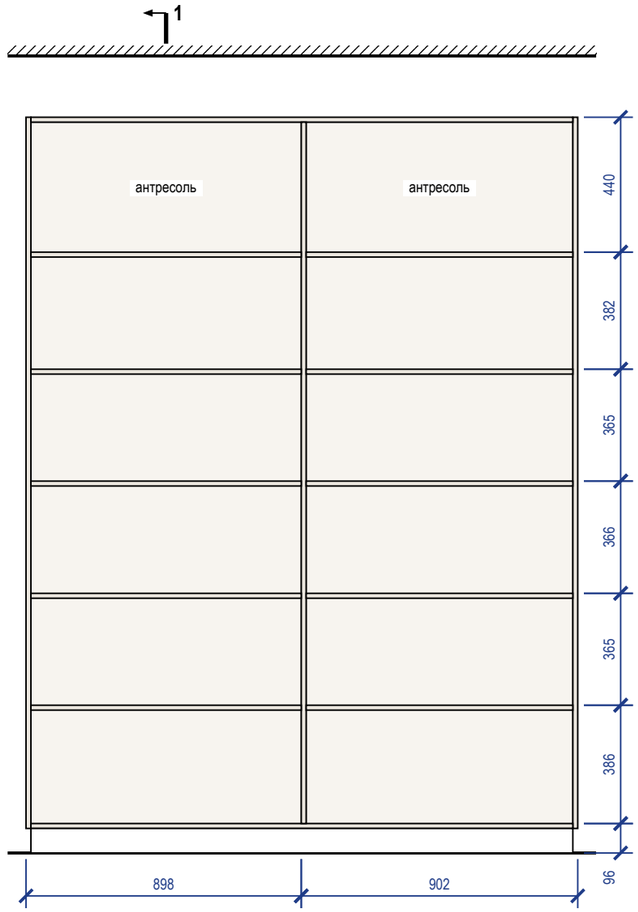



## Разрез 1-1

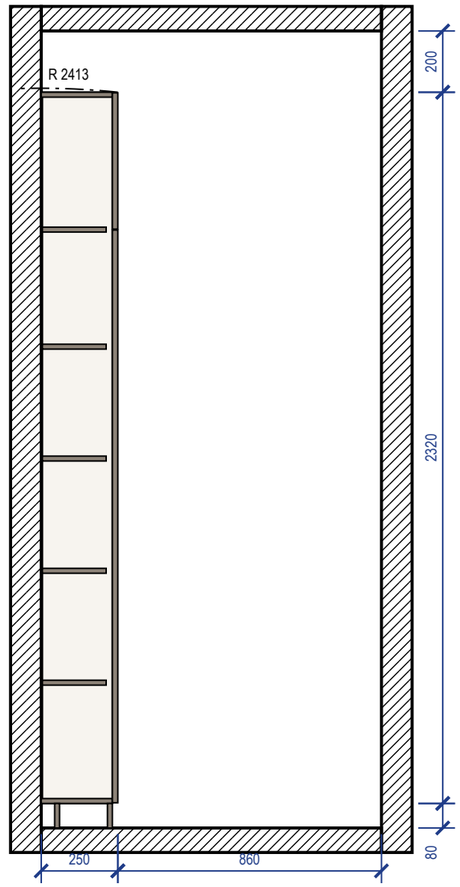


## Примечания

1. Размеры — в мм по чистовой отделке; изделие 1800×250×2400 (Ш×Г×В). Перед раскроем — контрольный замер цеха после чистовой отделки стен, пола и потолка.
2. Корпус — ЛДСП 16 мм, задняя стенка ХДФ 4 мм в паз, цоколь 80 мм на регулируемых опорах; фасады — МДФ, эмаль матовая 18 мм накладные, цвет — по колерной карте; петли с доводчиком: фасад 1869 мм — 4 петли, фасад 445 мм — 2 петли.
3. Кромка: скрытые торцы 0,4 мм, видимые 2 мм (ПВХ/АБС).
4. Номинальные зазоры: между фасадами 3 мм, фасад — стена и фасад — потолок не менее 3 мм, фасад ящика — стойка 2 мм.
5. Присадка по 32-й системе — выполняет цех.
6. Зазор до потолка 200 мм.
7. Подъём корпуса: диагональ боковины $\sqrt{(2400^2 + 250^2)} = 2413$ мм < 2600 мм до потолка — корпус собирается лёжа и поднимается поворотом.
8. Крепление к стене от опрокидывания: крепление к стене, 4 точки; основание стены и шаг анкеров — монтажная схема шкафов.
9. Проход перед изделием 860 мм показан на разрезе 1-1.


## 3D орто

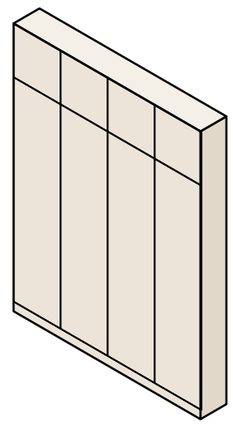


| | | | | | | | |
|---|---|---|---|---|---|---|---|
| | | | | | Проект: Четырёхкомнатная квартира | | |
| | Лист | № док. | Подпись | Дата | | | |
| Дизайнер | Кырлан А.С. | | | 05.10.26 | Система хранения M_18 | Стадия | Лист | Листов |
| | | | | | | П | Д_6 | 111 |

выпуск 05.10.2026 № 05166c8858 · стр. 99 из 111


## Вид с фасадами

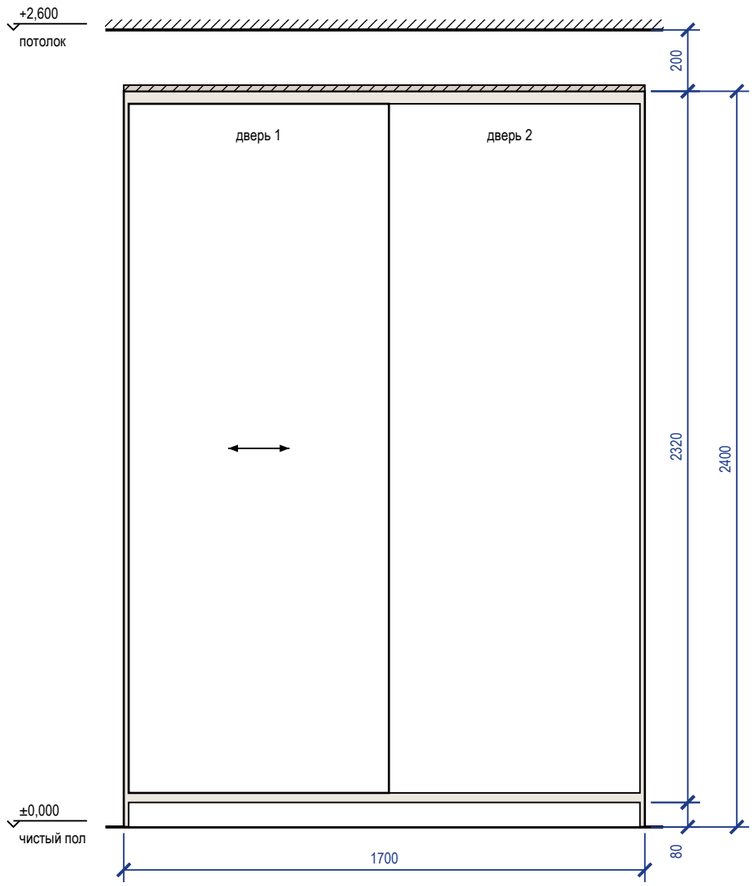



## Вид без фасадов

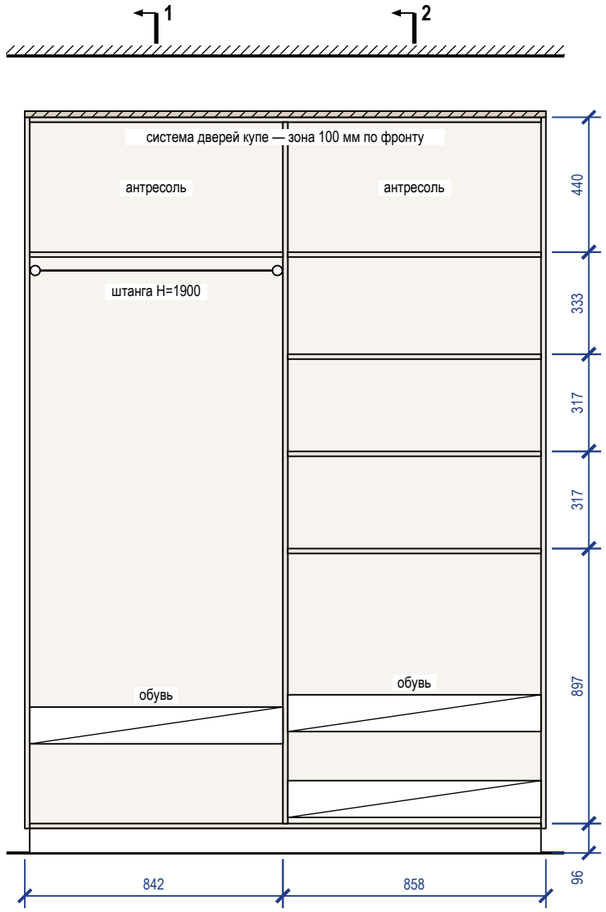


## Разрез 1-1

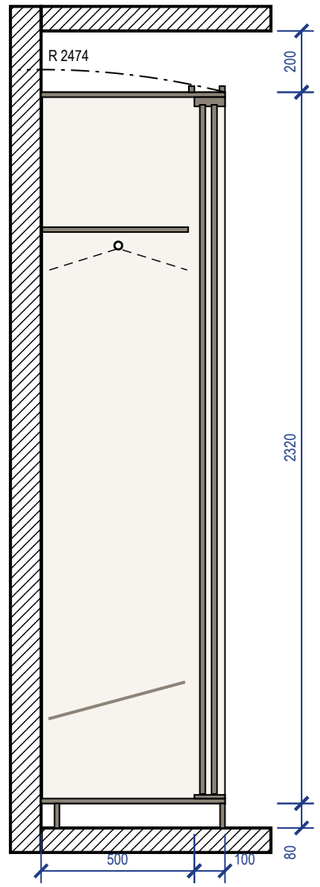



## Разрез 2-2

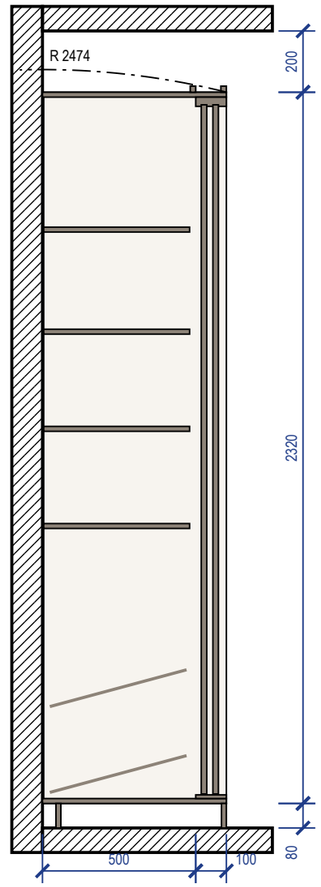


### Примечания

1. Размеры — в мм по чистовой отделке; изделие 1700×600×2400 (Ш×Г×В). Перед раскроем — контрольный замер цеха после чистовой отделки стен, пола и потолка.
2. Корпус — ЛДСП 16 мм, задняя стенка ХДФ 4 мм в паз, цоколь 80 мм на регулируемых опорах; двери купе — ЛДСП 10 мм в алюминиевом профиле, нахлёст 30 мм, ширина двери 849 мм, высота — проём минус 40 мм; цвет — по колерной карте.
3. Кромка: скрытые торцы 0,4 мм, видимые 2 мм (ПВХ/АБС).
4. Номинальные зазоры: дверь купе — боковина 3 мм, фасад ящика — стойка 2 мм; ящики внутри купе — с накладкой 30 мм на стойке со стороны нахлёста дверей.
5. Ящики — направляющие полного выдвижения NL 450 (внутренняя глубина 496 мм ≥ NL + 3); присадка по 32-й системе — выполняет цех.
6. Компенсатор 20 мм — короб из ЛДСП по фронту и торцам, подгоняется к потолку при монтаже (припуск 20 мм), крепится к корпусу и к потолку.
7. Подъём корпуса: диагональ боковины $\sqrt{(2400^2 + 600^2)} = 2474$ мм < 2600 мм до потолка — корпус собирается лёжа и поднимается поворотом.
8. Крепление к стене от опрокидывания: крепление к стене, 3 точки; основание стены и шаг анкеров — монтажная схема шкафов.

## 3D орто

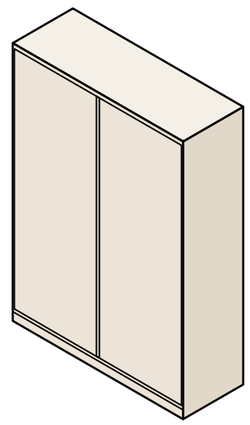


| | | | | | |
|---|---|---|---|---|---|
| | | | | | Проект: Четырёхкомнатная квартира |
| | Лист | № док. | Подпись | Дата | |
| Дизайнер | Кырлан А.С. | | | 05.10.26 | Шкаф-купе М_28 |


| Стадия | Лист | Листов |
|---|---|---|
| П | Д_7 | 111 |

выпуск 05.10.2026 № 05166c8858 · стр. 100 из 111


**Общий вид**

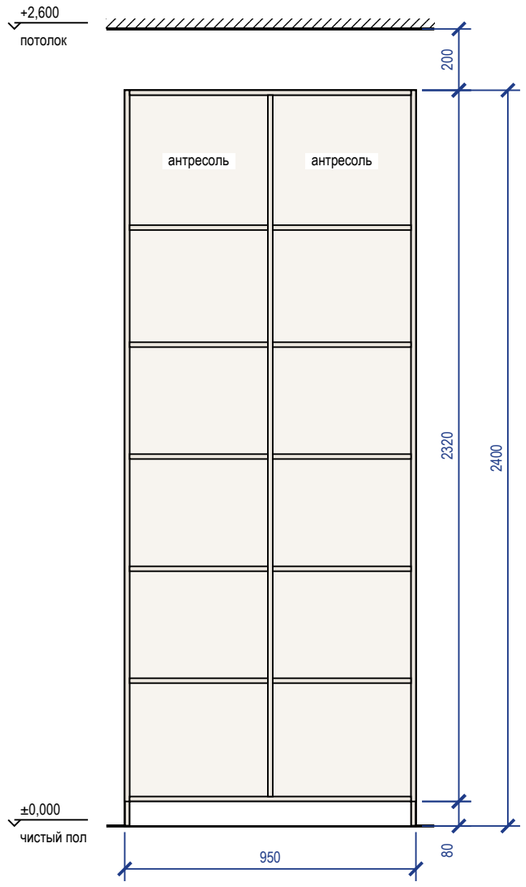


**Наполнение, размеры в свету**

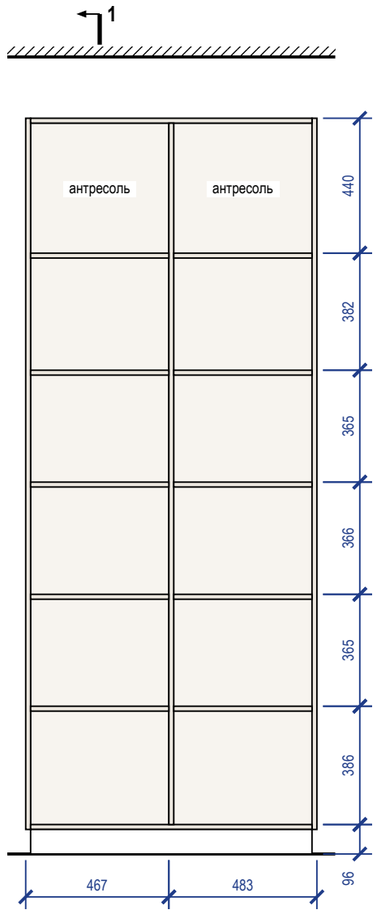



**Разрез 1-1**

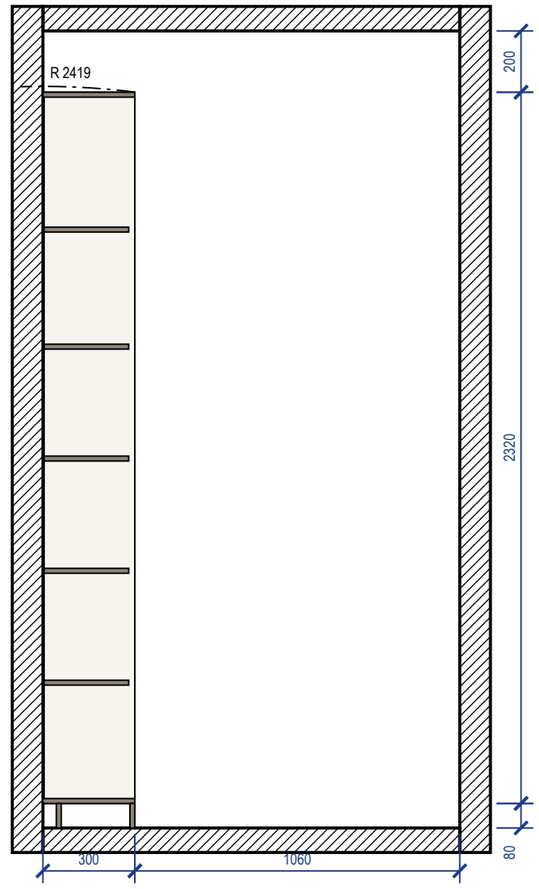


## Примечания

1. Размеры — в мм по чистовой отделке; изделие 950×300×2400 (Ш×Г×В). Перед раскроем — контрольный замер цеха после чистовой отделки стен, пола и потолка.
2. Корпус — ЛДСП 16 мм, задняя стенка ХДФ 4 мм в паз, цоколь 80 мм на регулируемых опорах; открытая система без фасадов, ящики с фасадами.
3. Кромка: скрытые торцы 0,4 мм, видимые 2 мм (ПВХ/АБС).
4. Номинальные зазоры: между фасадами ящиков 3 мм, фасад ящика — стойка 2 мм.
5. Ящики — направляющие полного выдвижения NL 270 (внутренняя глубина 296 мм ≥ NL + 3); присадка по 32-й системе — выполняет цех.
6. Зазор до потолка 200 мм.
7. Подъём корпуса: диагональ боковины $\sqrt{(2400^2 + 300^2)} = 2419$ мм < 2600 мм до потолка — корпус собирается лёжа и поднимается поворотом.
8. Крепление к стене от опрокидывания: крепление к стене, 3 точки; основание стены и шаг анкеров — монтажная схема шкафов.
9. Проход перед изделием 1060 мм показан на разрезе 1-1.

**3D орто**

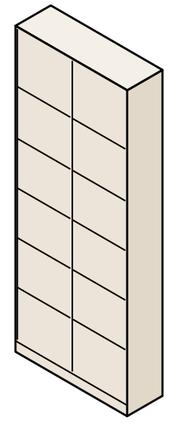


| | | | | | |
|---|---|---|---|---|---|
| | | | | | Проект: Четырёхкомнатная квартира |
| | Лист | № док. | Подпись | Дата | |
| Дизайнер | Кырлан А.С. | | | 05.10.26 | Система хранения М_31 |


| Стадия | Лист | Листов |
|---|---|---|
| П | Д_8 | 111 |

выпуск 05.10.2026 № 05166c8858 · стр. 101 из 111


## Общий вид

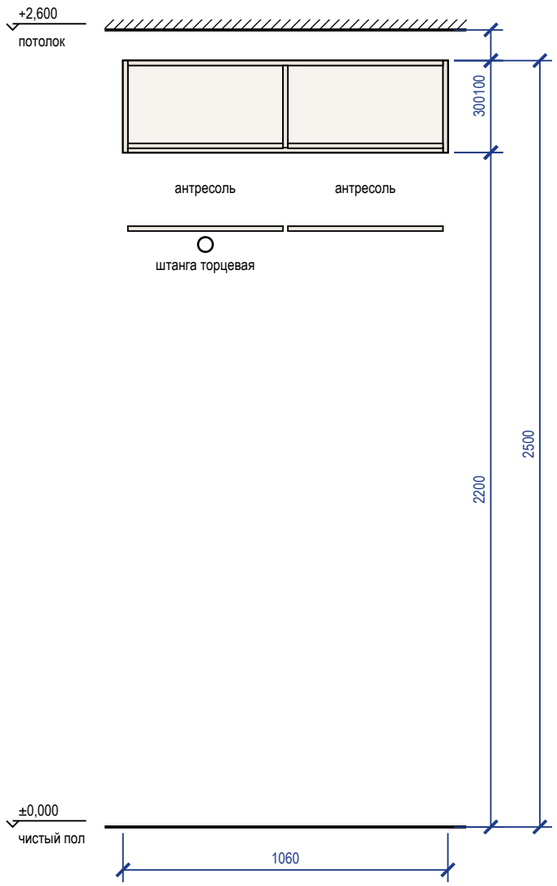



## Наполнение, размеры в свету

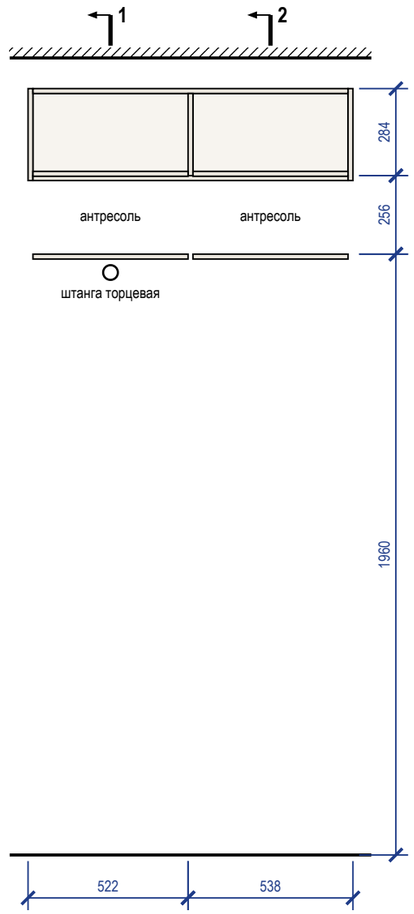


## Разрез 1-1

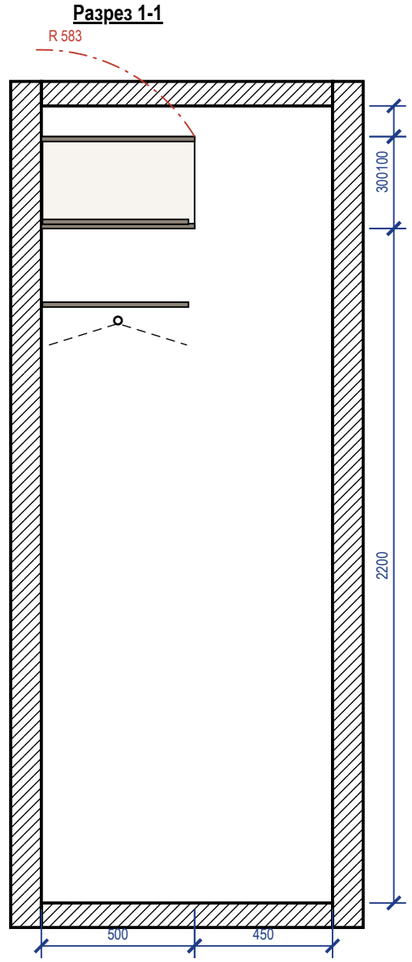



## Разрез 2-2

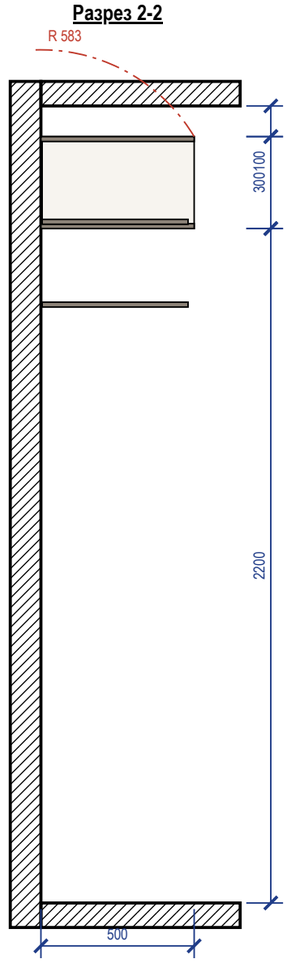


### Примечания

1. Размеры — в мм по чистовой отделке; изделие 1060×500×300 (Ш×Г×В). Перед раскроем — контрольный замер цеха после чистовой отделки стен, пола и потолка.
2. Корпус — ЛДСП 16 мм, задняя стенка ХДФ 4 мм в паз, цоколь 0 мм на регулируемых опорах; открытая система без фасадов, ящики с фасадами.
3. Кромка: скрытые торцы 0,4 мм, видимые 2 мм (ПВХ/АБС).
4. Номинальные зазоры: между фасадами ящиков 3 мм, фасад ящика — стойка 2 мм.
5. Ящики — направляющие полного выдвижения NL 450 (внутренняя глубина 496 мм ≥ NL + 3); присадка по 32-й системе — выполняет цех.
6. Зазор до потолка 100 мм — закрыть планкой в цвет корпуса при монтаже.
7. Подъём корпуса (траектория на виде — красная: корпус не проходит под потолком): диагональ боковины $\sqrt{(300^2 + 500^2)} = 583$ мм > 400 мм до потолка — поднять собранный корпус нельзя: высота корпуса не более 0 мм, остальное — компенсатор, либо сборка стоя на месте.
8. Крепление к стене от опрокидывания: крепление к стене, 4 точки; основание стены и шаг анкеров — монтажная схема шкафов.
9. Проход перед изделием 450 мм показан на разрезе 1-1: меньше 600 мм — глубину уменьшить (торцевые штанги при глубине 350–450 мм) или изменить расстановку.

## 3D орто

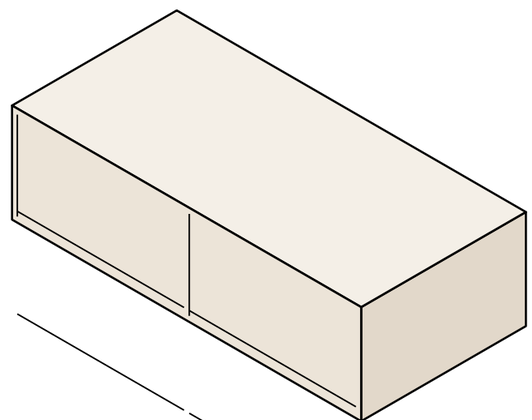


| | | | | | |
|---|---|---|---|---|---|
| | | | | | Проект: Четырёхкомнатная квартира |
| | Лист | № док. | Подпись | Дата | |
| Дизайнер | Кырлан А.С. | | | 05.10.26 | Система хранения M_32 |


| Стадия | Лист | Листов |
|---|---|---|
| П | Д_9 | 111 |

выпуск 05.10.2026 № 05166c8858 · стр. 102 из 111


## Вид с фасадами

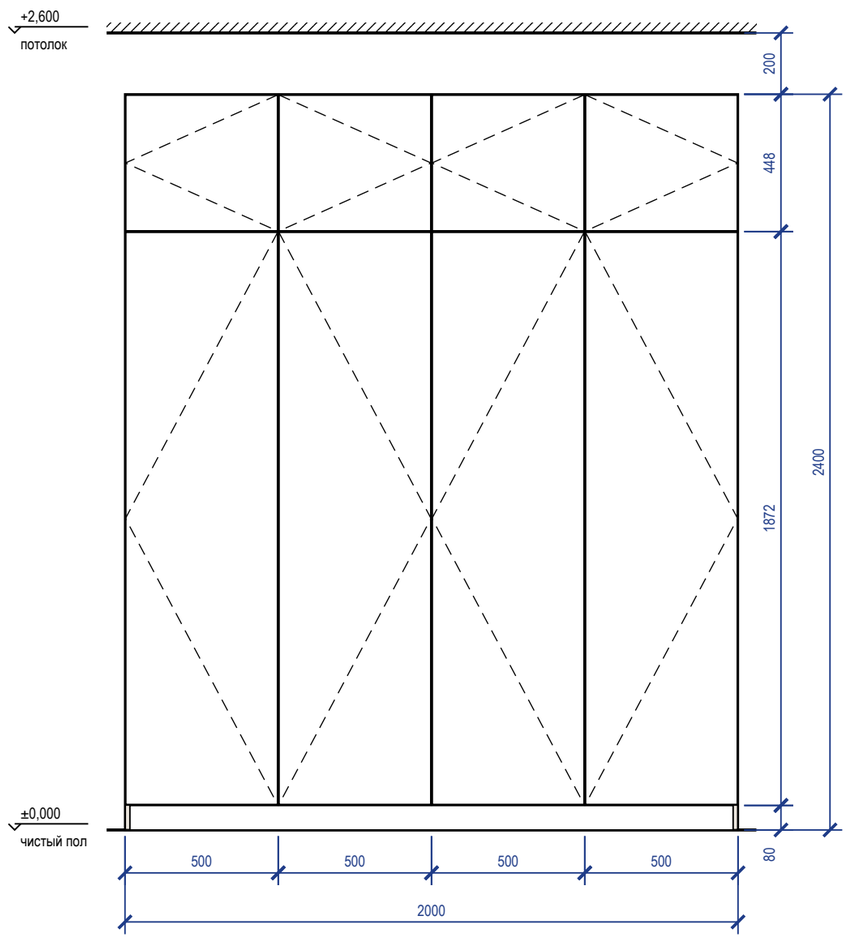



## Вид без фасадов

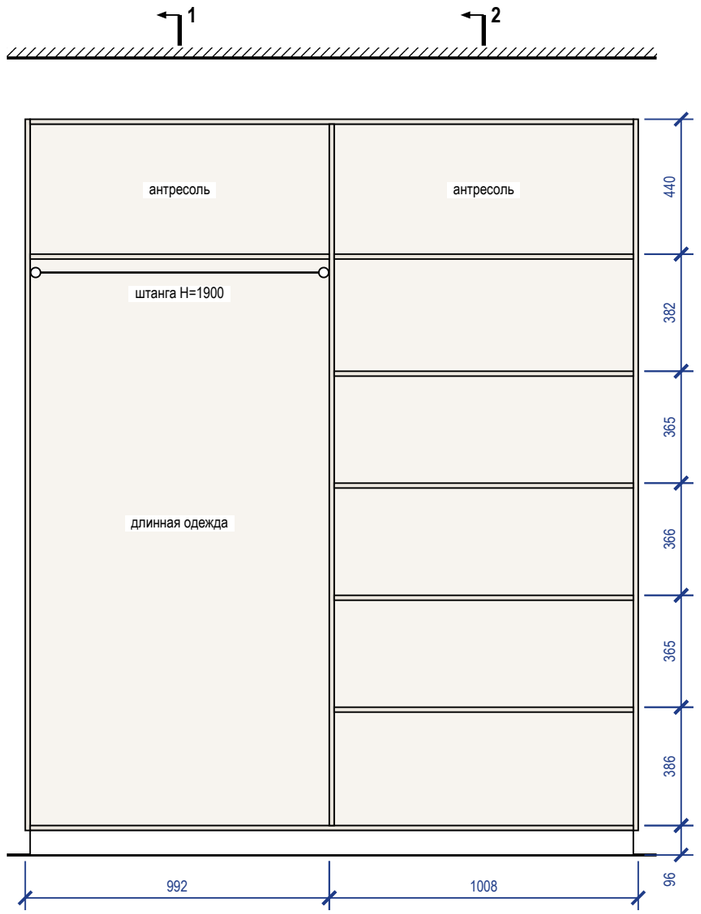


## Разрез 1-1

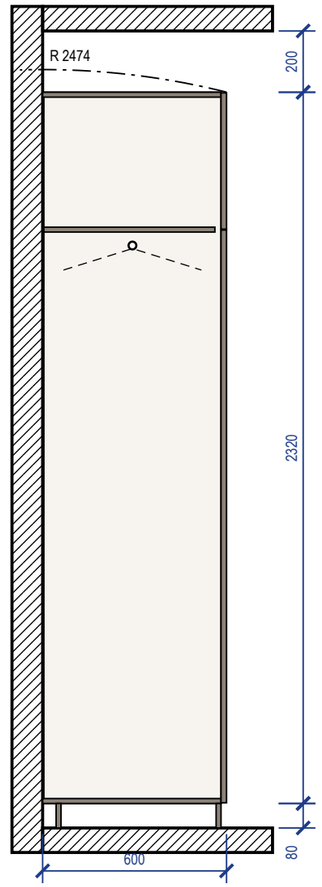



## Разрез 2-2

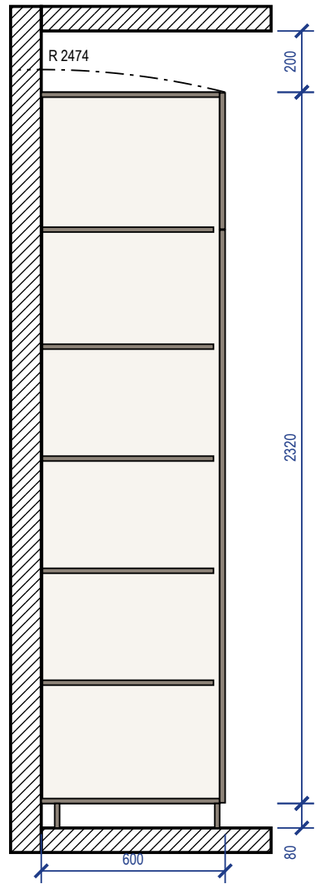


### Примечания

1. Размеры — в мм по чистовой отделке; изделие 2000×600×2400 (Ш×Г×В). Перед раскроем — контрольный замер цеха после чистовой отделки стен, пола и потолка.
2. Корпус — ЛДСП 16 мм, задняя стенка ХДФ 4 мм в паз, цоколь 80 мм на регулируемых опорах; фасады — МДФ, эмаль матовая 18 мм накладные, цвет — по колерной карте; петли с доводчиком: фасад 1869 мм — 4 петли, фасад 445 мм — 2 петли.
3. Кромка: скрытые торцы 0,4 мм, видимые 2 мм (ПВХ/АБС).
4. Номинальные зазоры: между фасадами 3 мм, фасад — стена и фасад — потолок не менее 3 мм, фасад ящика — стойка 2 мм.
5. Ящики — направляющие полного выдвижения NL 550 (внутренняя глубина 578 мм ≥ NL + 3); присадка по 32-й системе — выполняет цех.
6. Зазор до потолка 200 мм.
7. Подъём корпуса: диагональ боковины $\sqrt{(2400^2 + 600^2)} = 2474$ мм < 2600 мм до потолка — корпус собирается лёжа и поднимается поворотом.
8. Крепление к стене от опрокидывания: уголок к стене, 3 шт.; основание стены и шаг анкеров — монтажная схема шкафов.


## 3D орто

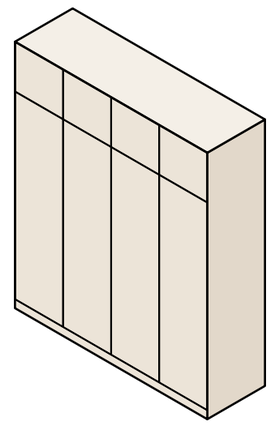


| | | | | | | | |
|---|---|---|---|---|---|---|---|
| | | | | | Проект: Четырёхкомнатная квартира | | |
| | Лист | № док. | Подпись | Дата | | | |
| Дизайнер | Кырлан А.С. | | | 05.10.26 | Шкаф распашной М_34 | Стадия | Лист | Листов |
| | | | | | | П | Д_10 | 111 |

выпуск 05.10.2026 № 05166c8858 · стр. 103 из 111


## Общий вид

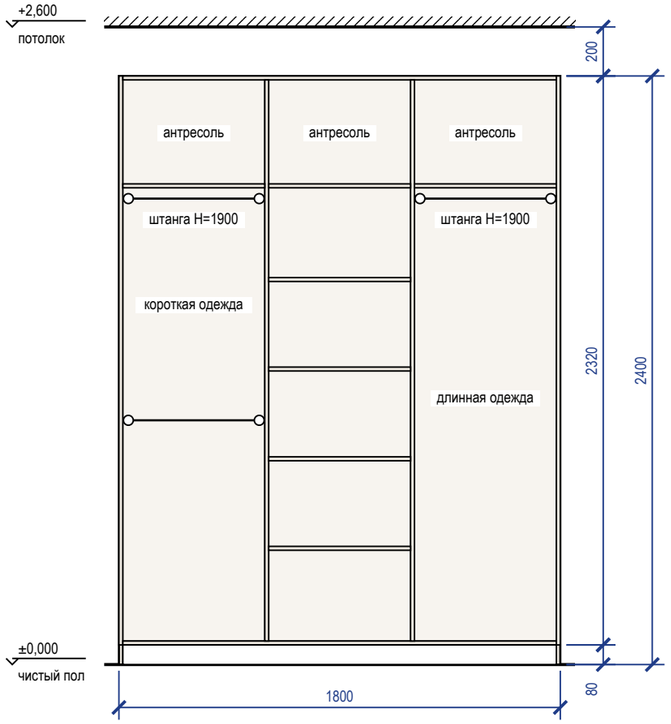



## Наполнение, размеры в свету

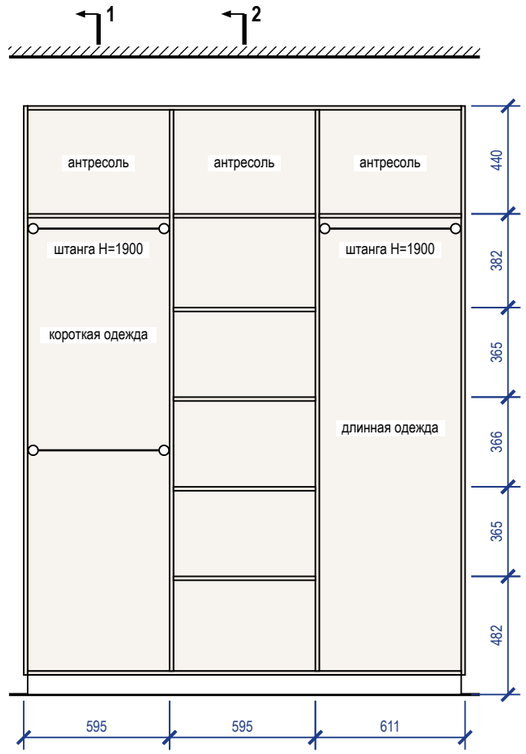


## Разрез 1-1

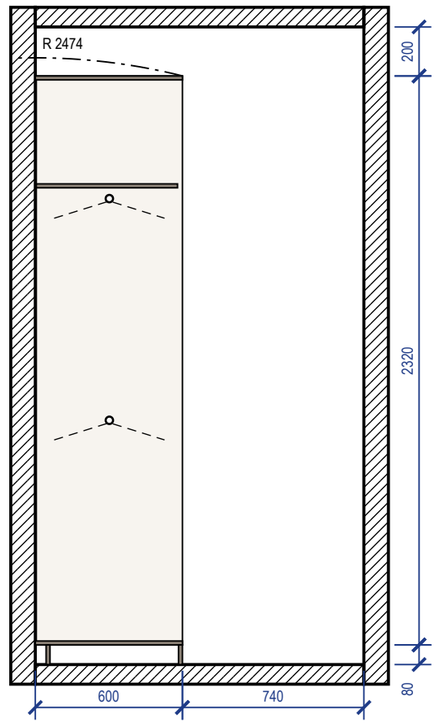



## Разрез 2-2

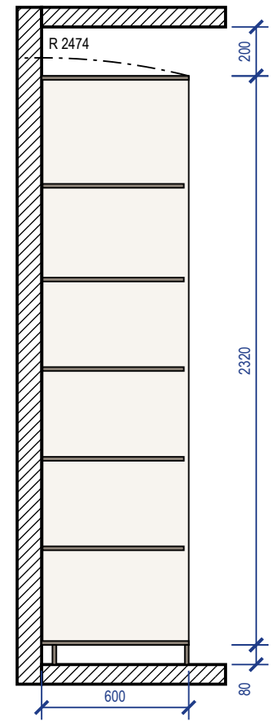


### Примечания

1. Размеры — в мм по чистовой отделке; изделие 1800×600×2400 (Ш×Г×В). Перед раскроем — контрольный замер цеха после чистовой отделки стен, пола и потолка.
2. Корпус — ЛДСП 16 мм, задняя стенка ХДФ 4 мм в паз, цоколь 80 мм на регулируемых опорах; открытая система без фасадов, ящики с фасадами.
3. Кромка: скрытые торцы 0,4 мм, видимые 2 мм (ПВХ/АБС).
4. Номинальные зазоры: между фасадами ящиков 3 мм, фасад ящика — стойка 2 мм.
5. Ящики — направляющие полного выдвижения NL 550 (внутренняя глубина 596 мм ≥ NL + 3); присадка по 32-й системе — выполняет цех.
6. Зазор до потолка 200 мм.
7. Подъём корпуса: диагональ боковины $\sqrt{(2400^2 + 600^2)} = 2474$ мм < 2600 мм до потолка — корпус собирается лёжа и поднимается поворотом.
8. Крепление к стене от опрокидывания: крепление к стене, 4 точки; основание стены и шаг анкеров — монтажная схема шкафов.
9. Проход перед изделием 740 мм показан на разрезе 1-1.


## 3D орто

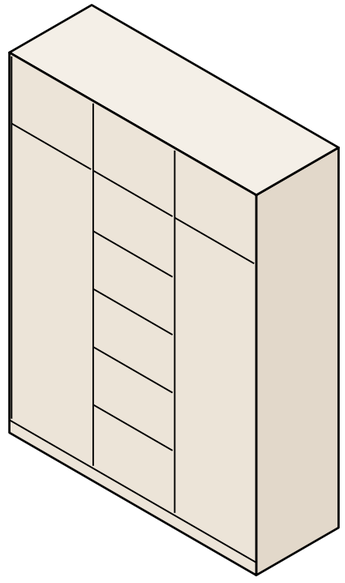


| | | | | | |
|---|---|---|---|---|---|
| | | | | | Проект: Четырёхкомнатная квартира |
| | Лист | № док. | Подпись | Дата | |
| Дизайнер | Кырлан А.С. | | | 05.10.26 | Система хранения M_38 |
| | | | | | Стадия: П; Лист: Д_11; Листов: 111 |

выпуск 05.10.2026 № 05166c8858 · стр. 104 из 111


**Общий вид**

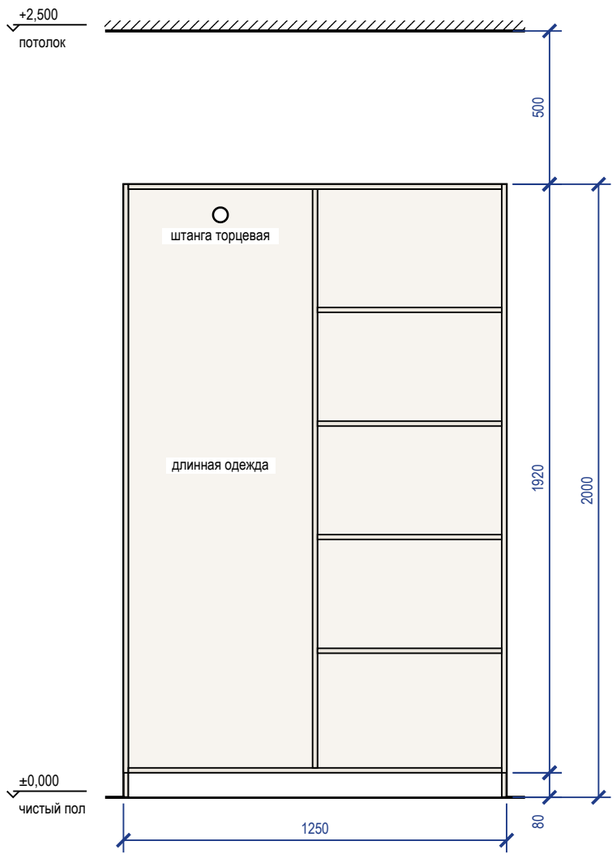



**Наполнение, размеры в свету**

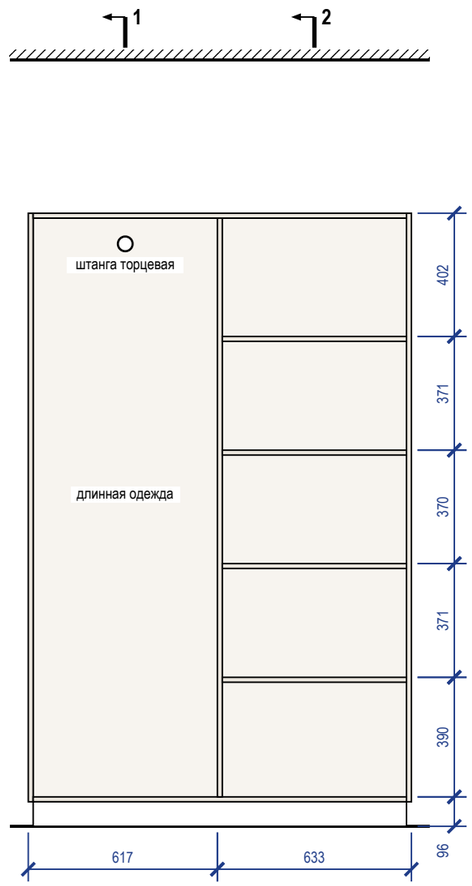


**Разрез 1-1**

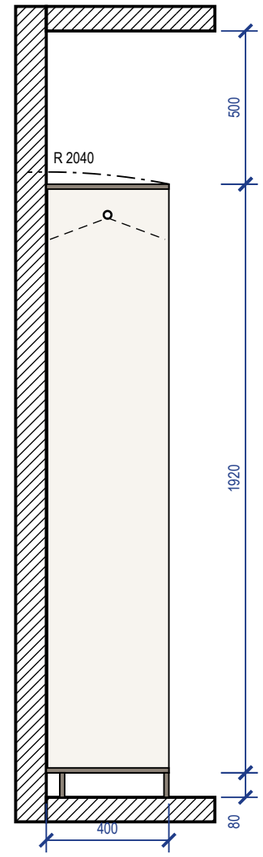



**Разрез 2-2**

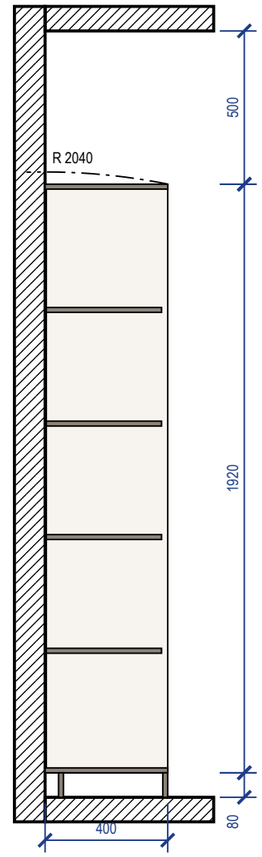


## Примечания

1. Размеры — в мм по чистовой отделке; изделие 1250×400×2000 (Ш×Г×В). Перед раскроем — контрольный замер цеха после чистовой отделки стен, пола и потолка.
2. Корпус — ЛДСП 16 мм, задняя стенка ХДФ 4 мм в паз, цоколь 80 мм на регулируемых опорах; открытая система без фасадов, ящики с фасадами.
3. Кромка: скрытые торцы 0,4 мм, видимые 2 мм (ПВХ/АБС).
4. Номинальные зазоры: между фасадами ящиков 3 мм, фасад ящика — стойка 2 мм.
5. Ящики — направляющие полного выдвижения NL 350 (внутренняя глубина 396 мм ≥ NL + 3); присадка по 32-й системе — выполняет цех.
6. Зазор до потолка 500 мм.
7. Подъём корпуса: диагональ боковины $\sqrt{(2000^2 + 400^2)} = 2040$ мм < 2500 мм до потолка — корпус собирается лёжа и поднимается поворотом.
8. Крепление к стене от опрокидывания: крепление к стене, 3 точки; основание стены и шаг анкеров — монтажная схема шкафов.

**3D орто**

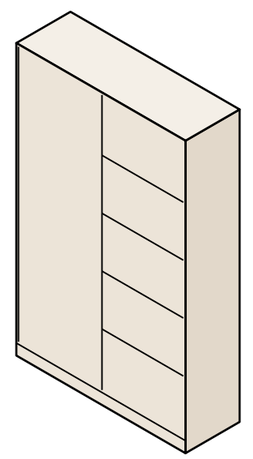


| | | | | | |
|---|---|---|---|---|---|
| | | | | | Проект: Четырёхкомнатная квартира |
| | Лист | № док. | Подпись | Дата | |
| Дизайнер | Кырлан А.С. | | | 05.10.26 | Система хранения М_39 |


| Стадия | Лист | Листов |
|---|---|---|
| П | Д_12 | 111 |

выпуск 05.10.2026 № 0516cc8858 · стр. 105 из 111


## Общий вид

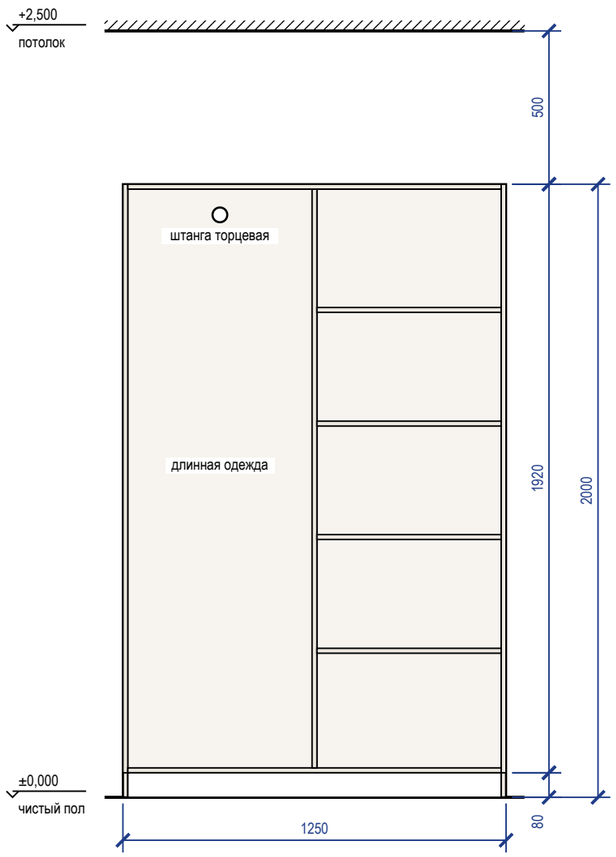



## Наполнение, размеры в свету

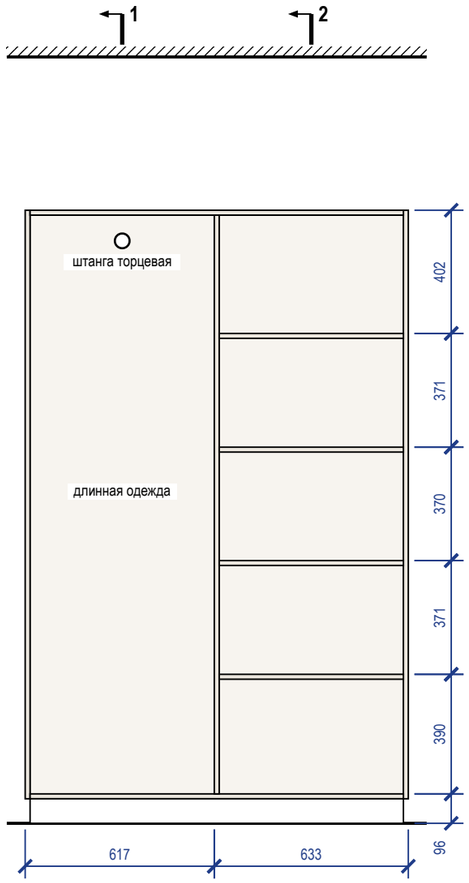


## Разрез 1-1

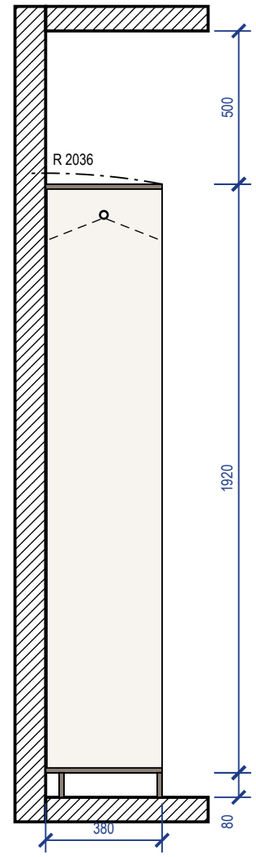



## Разрез 2-2

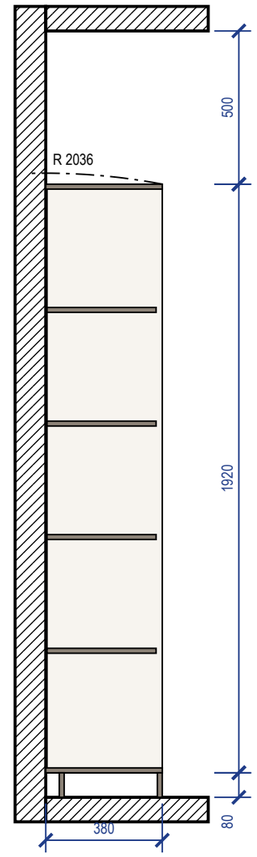


### Примечания

1. Размеры — в мм по чистовой отделке; изделие 1250×380×2000 (Ш×Г×В). Перед раскроем — контрольный замер цеха после чистовой отделки стен, пола и потолка.
2. Корпус — ЛДСП 16 мм, задняя стенка ХДФ 4 мм в паз, цоколь 80 мм на регулируемых опорах; открытая система без фасадов, ящики с фасадами.
3. Кромка: скрытые торцы 0,4 мм, видимые 2 мм (ПВХ/АБС).
4. Номинальные зазоры: между фасадами ящиков 3 мм, фасад ящика — стойка 2 мм.
5. Ящики — направляющие полного выдвижения NL 350 (внутренняя глубина 376 мм ≥ NL + 3); присадка по 32-й системе — выполняет цех.
6. Зазор до потолка 500 мм.
7. Подъём корпуса: диагональ боковины $\sqrt{(2000^2 + 380^2)} = 2036$ мм < 2500 мм до потолка — корпус собирается лёжа и поднимается поворотом.
8. Крепление к стене от опрокидывания: крепление к стене, 3 точки; основание стены и шаг анкеров — монтажная схема шкафов.

## 3D орто

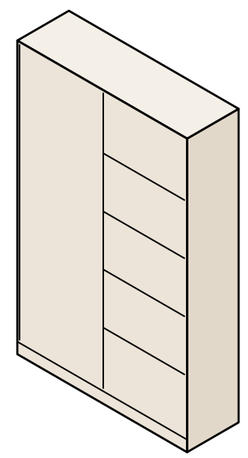


| | | | | | |
|---|---|---|---|---|---|
| | | | | | Проект: Четырёхкомнатная квартира |
| | Лист | № док. | Подпись | Дата | |
| Дизайнер | Кырлан А.С. | | | 05.10.26 | Система хранения М_40 |


| Стадия | Лист | Листов |
|---|---|---|
| П | Д_13 | 111 |

выпуск 05.10.2026 № 05166c8858 · стр. 106 из 111


## Вид с фасадами

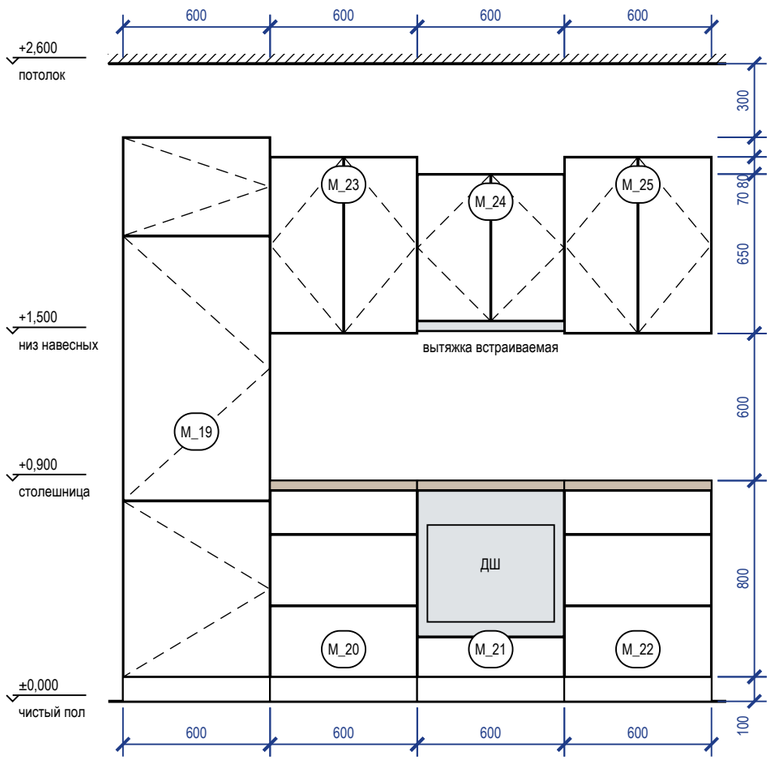



## Вид без фасадов (наполнение, выводы)

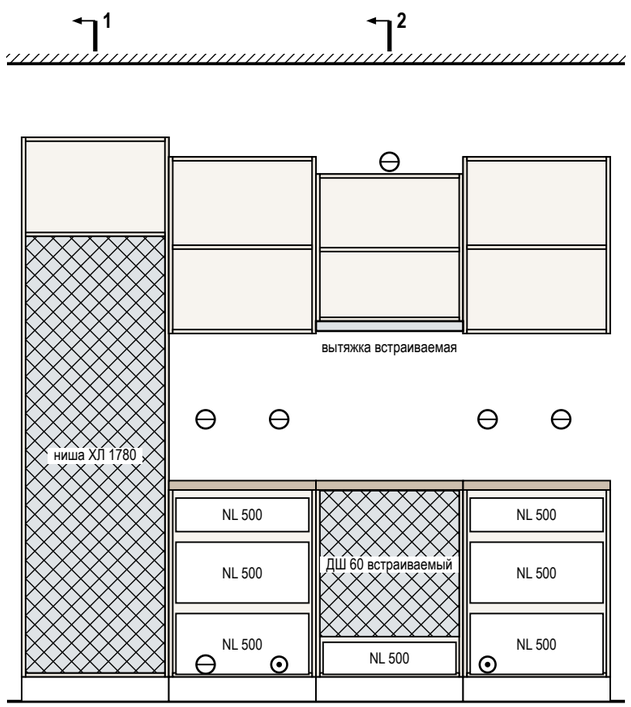



## Разрез 1-1

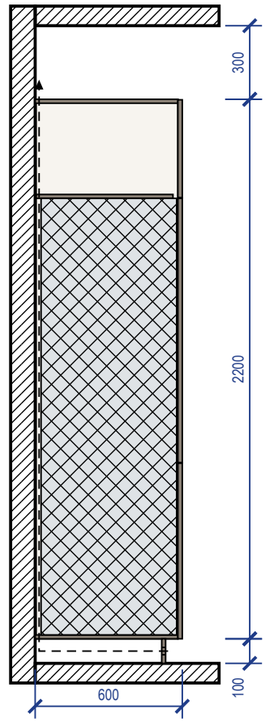


## Разрез 2-2

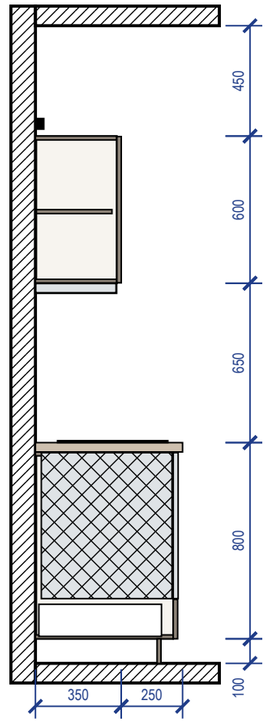


## 3D орто

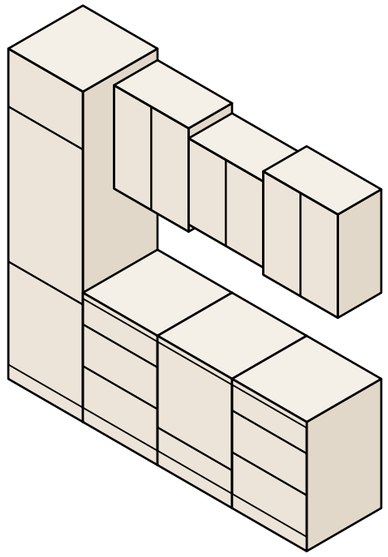

## Примечания


1. Размеры — в мм по чистовой отделке, вид из помещения; марки — как на плане расстановки. Перед раскроем — контрольный замер цеха после фартука и пола.
2. Корпуса — ЛДСП 16 мм, задняя стенка ХДФ 4 мм; фасады — МДФ, эмаль матовая 18 мм, цвет по колерной карте; столешница 38 мм, свес 20 мм; цоколь 100 мм.
3. Кромка: скрытые торцы 0,4 мм, видимые 2 мм. Номинальные зазоры: между фасадами 3 мм, фасад — столешница 3 мм, фасад — стена не менее 3 мм.
4. Ящики полного выдвижения и петли — с доводчиком; присадка по 32-й системе — выполняет цех.
5. Вытяжка встраивается в навесной модуль над варочной: её низ 610 мм над панелью — меньше 650 мм, модуль поднять или принять вытяжку с допуском по паспорту модели.
6. Ниши техники (холодильник — ориентир 1780 мм) — по монтажным схемам выбранных моделей: решётка в цоколе и канал за пеналом холодильника, зазор за духовым шкафом, фасад ПММ на двери машины.

| | | | | | |
|---|---|---|---|---|---|
| | | | | | Проект: Четырёхкомнатная квартира |
| | Лист | № док. | Подпись | Дата | Кухня (пом. 6). Развёртка гарнитура |
| Дизайнер | Кырлан А.С. | | | 05.10.26 | |


| Стадия | Лист | Листов |
|---|---|---|
| П | Д_14 | 111 |

выпуск 05.10.2026 № 05166c8858 · стр. 107 из 111


**Вид с фасадами**

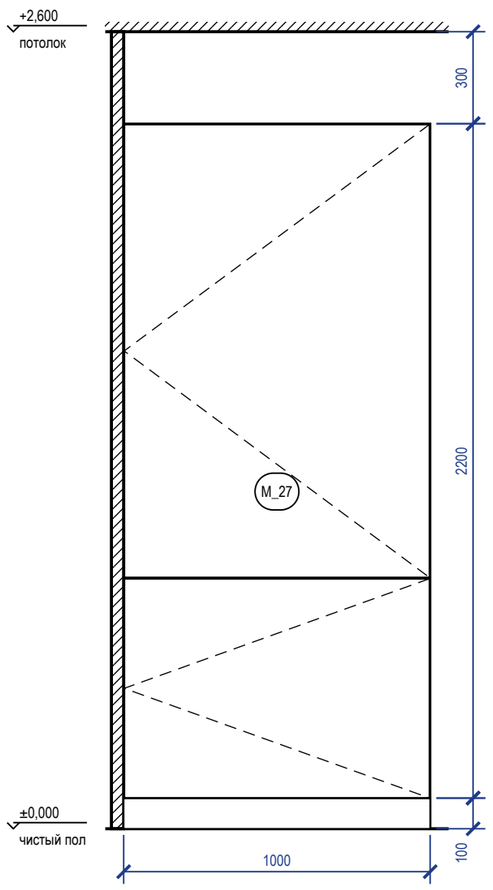



**Вид без фасадов (наполнение, выводы)**

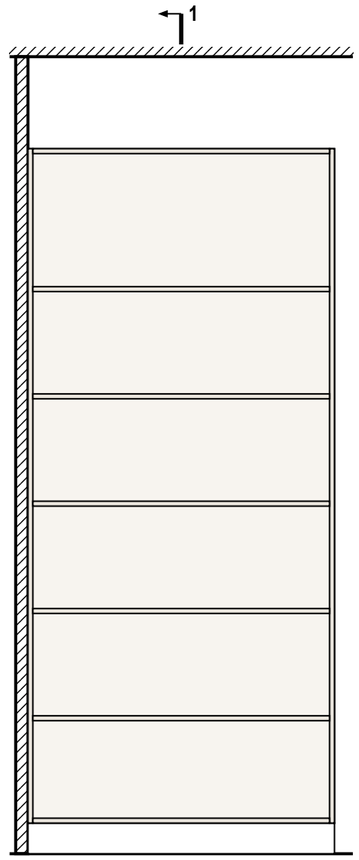


**Разрез 1-1**

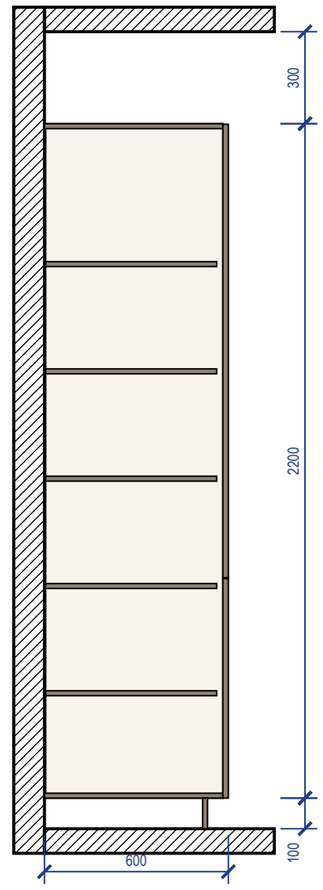


**3D орто**

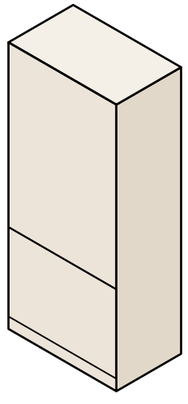

## Примечания

1. Размеры — в мм по чистовой отделке, вид из помещения; марки — как на плане расстановки. Перед раскроем — контрольный замер цеха после фартука и пола.
2. Корпуса — ЛДСП 16 мм, задняя стенка ХДФ 4 мм; фасады — МДФ, эмаль матовая 18 мм, цвет по колерной карте; столешница 38 мм, свес 20 мм; цоколь 100 мм.
3. Кромка: скрытые торцы 0,4 мм, видимые 2 мм. Номинальные зазоры: между фасадами 3 мм, фасад — столешница 3 мм, фасад — стена не менее 3 мм.
4. Ящики полного выдвижения и петли — с доводчиком; присадка по 32-й системе — выполняет цех.
5. Ниши техники — по монтажным схемам выбранных моделей: решётка в цоколе и канал за пеналом холодильника, зазор за духовым шкафом, фасад ПММ на двери машины.

| | | | | | |
|---|---|---|---|---|---|
| | | | | | Проект: Четырёхкомнатная квартира |
| | Лист | № док. | Подпись | Дата | Кухня (пом. 6). Развёртка гарнитура |
| Дизайнер | Кырлан А.С. | | | 05.10.26 | |

| Стадия | Лист | Листов |
|---|---|---|
| П | Д_15 | 111 |

выпуск 05.10.2026 № 05166c8858 · стр. 108 из 111

## Ведомость отделки помещений (форма 1 прил. А ГОСТ 21.501-2018). Лист 1 из 2

| № | Наименование помещения | Потолок | | | Стены и перегородки | | | Низ стен (плинтус) | | | Пол | | Примечание |
|---|---|---|---|---|---|---|---|---|---|---|---|---|---|
| | | Вид отделки | Код цвета | S, м² | Вид отделки | Код цвета | S, м² | Вид отделки | Код цвета | L, м | Вид отделки | S, м² | |
| 1 | Зал<br>18,16 м² | ГКЛ по каркасу П113, отм. +2,500; +2,600; окраска, Tikkurila Anti-Reflex 2, глубокоматовая, 2 слоя, подготовка Q3 | Tikkurila F497 | 18,16 | Окраска, Tikkurila Optiva 5 Matt, матовая, 2 слоя, подготовка К3<br>Акцент — стена А: окраска, Tikkurila Optiva 5 Matt, матовая, 3 слоя, подготовка К3 | Tikkurila F497<br>Tikkurila L481 | 25,94<br>13,55 | Плинтус МДФ h=80 мм, аналог: МДФ под окраску 80×16 мм | Tikkurila F497 | 16,6 | Инженерная доска, аналог: дуб натуральный брашированный, масло-воск, 14/4 мм, на клею; тип 1, отм. ЧП ±0,000 | 18,16 | Н стен 2500 (до потолка); колеруется в код стен, но по эмали на МДФ: сличать отдельным выкрасом на своей подложке (выкрас № 10); плинтус в цвет: стены |
| 2 | Ванная комната<br>5,57 м² | ГКЛВ по каркасу П113, отм. +2,500; окраска, Tikkurila Luja 7, матовая, 2 слоя, подготовка Q3 | Tikkurila F497 | 5,57 | Облицовка плиткой, аналог: керамогранит матовый, тон F497, 600×600×9 мм, клей C2 TE S1, затирка CG2WA | #F1F1EC | 22,35 | нет (облицовка от пола) | | | Аналог: керамогранит матовый R10, тон J484, 600×600×10 мм; тип 2, отм. ЧП −0,015 | 5,57 | Н стен 2515 (до потолка); тёплый пол; гидроизоляция обмазочная, 2 слоя, по всему помещению, с заведением на стены 200 мм, в душе — на 2100 мм и 500 мм за кабину (по пирогу пола); тест проливом и акт скрытых работ; облицовка от чистого пола до низа потолка; по ГКЛВ каркаса П113, влагостойкая окраска; Q3 |
| 3 | Тёмная комната<br>2,96 м² | ГКЛ по каркасу П113, отм. +2,600; окраска, Tikkurila Anti-Reflex 2, глубокоматовая, 2 слоя, подготовка Q3 | Tikkurila F497 | 2,96 | Окраска, Tikkurila Optiva 5 Matt, матовая, 2 слоя, подготовка К3 | Tikkurila F497 | 16,94 | Плинтус МДФ h=80 мм, аналог: МДФ под окраску 80×16 мм | Tikkurila F497 | 6,4 | Инженерная доска, аналог: дуб натуральный брашированный, масло-воск, 14/4 мм, на клею; тип 1, отм. ЧП ±0,000 | 2,96 | Н стен 2600 (до потолка); колеруется в код стен, но по эмали на МДФ: сличать отдельным выкрасом на своей подложке (выкрас № 10); плинтус в цвет: стены |
| 4 | Детская 1<br>17,51 м² | ГКЛ по каркасу П113, отм. +2,600; окраска, Tikkurila Anti-Reflex 2, глубокоматовая, 2 слоя, подготовка Q3 | Tikkurila F497 | 17,51 | Окраска, Tikkurila Joker, полуматовая, 2 слоя, подготовка К3 | Tikkurila F497 | 40,12 | Плинтус МДФ h=80 мм, аналог: МДФ под окраску 80×16 мм | Tikkurila F497 | 16,2 | Инженерная доска, аналог: дуб натуральный брашированный, масло-воск, 14/4 мм, на клею; тип 1, отм. ЧП ±0,000 | 17,51 | Н стен 2600 (до потолка); колеруется в код стен, но по эмали на МДФ: сличать отдельным выкрасом на своей подложке (выкрас № 10); плинтус в цвет: стены |
| 5 | Коридор<br>4,54 м² | ГКЛ по каркасу П113, отм. +2,600; окраска, Tikkurila Anti-Reflex 2, глубокоматовая, 2 слоя, подготовка Q3 | Tikkurila F497 | 4,54 | Окраска, Tikkurila Optiva 20 Semimatt, полуматовая, 2 слоя, подготовка К3 | Tikkurila J484 | 22,21 | Плинтус МДФ h=80 мм, аналог: МДФ под окраску 80×16 мм | Tikkurila J484 | 8,1 | Аналог: керамогранит матовый R10, тон V486, 600×600×10 мм; тип 3, отм. ЧП ±0,000 | 4,54 | Н стен 2600 (до потолка); колеруется в код стен, но по эмали на МДФ: сличать отдельным выкрасом на своей подложке (выкрас № 10); плинтус в цвет: стены |
| 6 | Кухня<br>15,19 м² | ГКЛ по каркасу П113, отм. +2,600; окраска, Tikkurila Luja 7, матовая, 2 слоя, подготовка Q3 | Tikkurila F497 | 15,19 | Окраска, Tikkurila Luja 7, полуматовая, 2 слоя, подготовка К3<br>Фартук кухни (стена А): облицовка керамогранитом, аналог: керамогранит матовый, тон F497, 600×600×9 мм, клей C2 TE S1, затирка CG2WA | Tikkurila F497<br>#F1F1EC | 34,48<br>1,11 | Плинтус МДФ h=80 мм, аналог: МДФ под окраску 80×16 мм | Tikkurila F497 | 13,8 | Инженерная доска, аналог: дуб натуральный брашированный, масло-воск, 14/4 мм, на клею; тип 4, отм. ЧП ±0,000 | 15,19 | Н стен 2600 (до потолка); гидроизоляция обмазочная, 2 слоя, с заведением на стены 200 мм (по пирогу пола); тест проливом и акт скрытых работ; влагостойкая полуматовая окраска (класс мокрого истирания 1 по EN 13300); категория К3 по СП 71.13330.2017, табл. 7.5; по ГКЛ каркаса П113, влагостойкая окраска; Q3 колеруется в код стен, но по эмали на МДФ: сличать отдельным выкрасом на своей подложке (выкрас № 10); плинтус в цвет: стены |

### Примечания

1. Ведомость продолжена на листе 2 из 2; итоги, сводка площадей и примечания — на последнем листе ведомости.

| | | | | | |
|---|---|---|---|---|---|
| | | | | | Проект: Четырёхкомнатная квартира |
| | Лист | № док. | Подпись | Дата | Ведомость отделки помещений. Лист 1 из 2 |
| Дизайнер | Кырлан А.С. | | | 05.10.26 | |

| Стадия | Лист | Листов |
|---|---|---|
| П | С1 | 111 |

выпуск 05.10.2026 № 05166c8858 · стр. 109 из 111

| Поз. | Наименование и техническая характеристика | Тип, марка, обозначение документа | Код продукции | Поставщик | Ед. изм. | Кол. | Образец | Примечание |
|---|---|---|---|---|---|---|---|---|
| | **Лакокрасочные материалы** | | | | | | | |
| 1 | Краска интерьерная водно-дисперсионная акриловая для стен, матовая, класс мокрого истирания 2 по EN 13300, база A; цвет Tikkurila F497 «Paper», колеровка машинная | Tikkurila Optiva 5 Matt | | Tikkurila | л | 25,2 | | поз. К1 колерной карты; пом. 1, 3, 8, 11, 12; S = 93,0 м² × 2 сл. × 0,12 л/м² = 22,3 л, +10 % и 0,5 л на подкраску → ≥ 25,1 л; тара 2 × 9 л + 2 × 2,7 л + 2 × 0,9 л |
| 2 | Краска интерьерная водно-дисперсионная акриловая для акцентных стен, матовая, класс мокрого истирания 2 по EN 13300, база C; цвет Tikkurila L481 «Silhouette», колеровка машинная | Tikkurila Optiva 5 Matt | | Tikkurila | л | 10,8 | | поз. К2 колерной карты; пом. 1, 11; S = 24,3 м² × 3 сл. × 0,12 л/м² = 8,7 л, +10 % и 0,5 л на подкраску → ≥ 10,1 л; тара 1 × 9 л + 2 × 0,9 л |
| 3 | Краска интерьерная водно-дисперсионная акриловая для потолков, глубокоматовая, класс мокрого истирания 2 по EN 13300, база A; цвет Tikkurila F497 «Paper», колеровка машинная | Tikkurila Anti-Reflex 2 | | Tikkurila | л | 22,5 | | поз. К3 колерной карты; пом. 1, 3, 4, 5, 7, 8, 9, 11, 12; S = 80,6 м² × 2 сл. × 0,12 л/м² = 19,3 л, +10 % и 0,5 л на подкраску → ≥ 21,8 л; тара 2 × 9 л + 1 × 2,7 л + 2 × 0,9 л |
| 4 | Краска интерьерная водно-дисперсионная акриловая для потолков, матовая, класс мокрого истирания 1 по EN 13300, база A; цвет Tikkurila F497 «Paper», колеровка машинная | Tikkurila Luja 7 | | Tikkurila | л | 8,1 | | поз. К5 колерной карты; пом. 2, 6, 10, 13; S = 25,8 м² × 2 сл. × 0,12 л/м² = 6,2 л, +10 % и 0,5 л на подкраску → ≥ 7,3 л; тара 3 × 2,7 л |
| 5 | Краска интерьерная водно-дисперсионная акриловая для стен, полуматовая, класс мокрого истирания 2 по EN 13300, база A; цвет Tikkurila F497 «Paper», колеровка машинная | Tikkurila Joker | | Tikkurila | л | 18,9 | | поз. К6 колерной карты; пом. 4, 9; S = 69,2 м² × 2 сл. × 0,12 л/м² = 16,6 л, +10 % и 0,5 л на подкраску → ≥ 18,8 л; тара 2 × 9 л + 1 × 0,9 л |
| 6 | Краска интерьерная водно-дисперсионная акриловая для стен, полуматовая, класс мокрого истирания 2 по EN 13300, база A; цвет Tikkurila J484 «Castle», колеровка машинная | Tikkurila Optiva 20 Semimatt | | Tikkurila | л | 13,5 | | поз. К7 колерной карты; пом. 5, 7; S = 46,0 м² × 2 сл. × 0,12 л/м² = 11,0 л, +10 % и 0,5 л на подкраску → ≥ 12,6 л; тара 1 × 9 л + 1 × 2,7 л + 2 × 0,9 л |
| 7 | Краска интерьерная водно-дисперсионная акриловая для стен, полуматовая, класс мокрого истирания 1 по EN 13300, база A; цвет Tikkurila F497 «Paper», колеровка машинная | Tikkurila Luja 7 | | Tikkurila | л | 14,4 | | поз. К9 колерной карты; пом. 6, 13; S = 51,0 м² × 2 сл. × 0,12 л/м² = 12,2 л, +10 % и 0,5 л на подкраску → ≥ 14,0 л; тара 1 × 9 л + 2 × 2,7 л |
| 8 | Акрилово-уретановая эмаль на водной основе, полуглянцевая в цвет Tikkurila F497 «Paper» — окраска плинтуса | аналог по характеристикам | | | л | 2,3 | | поз. К4; пом. 1, 3, 4, 6, 8, 9, 11, 12; L = 89,2 м, S = 8,6 м² × 2 сл. × 0,12 л/м² + 10 %; продукт подобрать в веере Tikkurila |
| 9 | Акрилово-уретановая эмаль на водной основе, полуглянцевая в цвет Tikkurila J484 «Castle» — окраска плинтуса | аналог по характеристикам | | | л | 0,5 | | поз. К8; пом. 5, 7; L = 16,8 м, S = 1,6 м² × 2 сл. × 0,12 л/м² + 10 %; продукт подобрать в веере Tikkurila |
| 10 | Грунтовка акриловая под окраску стен и потолков — из системы производителя краски | по системе краски | | | м² | 390 | | площадь окраски стен, акцентов и потолков; 1 слой перед окраской; расход — по ТУ грунтовки |
| | **Плитка и керамогранит** | | | | | | | |
| 11 | Керамогранит матовый R10, тон J484, 600.8×600.8 мм | аналог по характеристикам | | | м² | 10,47 | | шов 2 мм; Ванная комната, пол; Санузел, пол; по раскладке 26 шт (S = 6,88 м²), с запасом 29 шт |
| 12 | Керамогранит матовый, тон F497, 600.8×600.8 мм | аналог по характеристикам | | | м² | 63,17 | | шов 2 мм; Ванная комната, стены А–Г; Ванная комната, короб инсталляции; Санузел, стены А–Г; Санузел, короб инсталляции; по раскладке 157 шт (S = 34,22 м²), с запасом 175 шт |
| 13 | Керамогранит матовый R10, тон V486, 600.8×600.8 мм | аналог по характеристикам | | | м² | 15,88 | | шов 2 мм; Коридор, пол; Прихожая-коридор, пол; по раскладке 39 шт (S = 12,34 м²), с запасом 44 шт |
| 14 | Керамогранит матовый, тон F497, 600.8×600.8 мм | аналог по характеристикам | | | м² | 1,80 | | шов 2 мм; Кухня, фартук (ст. А); по раскладке 4 шт (S = 1,11 м²), с запасом 5 шт |
| 15 | Керамогранит матовый R11, тон V486, водопоглощение 0,5 % (BIa), противоскольжение R11, PEI IV | аналог по характеристикам | | | м² | 4,07 | | 13. Балкон 1, пол; раскладка не выполнена — S = 3,70 м² + 10 %; клей и затирка — по раскладке |
| 16 | Плинтус из керамогранита пола, подрезка 80 мм, верхняя кромка с запилом 45° | аналог по характеристикам | | | м² | 8,46 | | 13. Балкон 1, стены; раскладка не выполнена — S = 7,69 м² + 10 %; клей и затирка — по раскладке |
| | **Напольные покрытия** | | | | | | | |
| 17 | Дуб натуральный брашированный, масло-воск, 14/4 мм, эмиссия E1, укладка на клей | аналог по характеристикам | | | м² | 89,3 | | пом. 1, 3, 4, 6, 8, 9, 11, 12; S = 83,45 м² + 7 % (прямая укладка); к заказу — кратно упаковке |
| 18 | Клей для паркета и инженерной доски, эластичный (СМП / полиуретановый) | по рекомендации производителя доски | | | м² | 84 | | площадь приклейки; расход и шпатель — по ТУ клея |
| | **Погонажные изделия** | | | | | | | |
| 19 | Плинтус МДФ под окраску 80×16 мм, крепление к стене, окраска в цвет Tikkurila F497 | аналог по характеристикам | | | м | 117 | | пом. 1, 3, 4, 5, 6, 7, 8, 9, 11, 12; L = 106,0 м (периметр без дверных проёмов) + 10 % на подрезку; в штуках — по длине планки |
| 20 | Плинтус из керамогранита пола, подрезка 80 мм, верхняя кромка с запилом 45°, h = 80 мм, крепление к стене | аналог по характеристикам | | | м | 9 | | пом. 13; L = 7,7 м (периметр без дверных проёмов) + 10 % на подрезку; в штуках — по длине планки |
| | **Смеси и материалы для облицовки** | | | | | | | |
| 21 | Затирка для швов плитки, класс CG2WA по EN 13888 | аналог: Mapei Ultracolor 133 | | аналог: | кг | 5,7 | | по раскладке (a+b)/(a·b) × шов × t × 1,6 + 10 %; в т. ч. 0,1 кг — позиции раскладки без марки |
| 22 | Клей плиточный C2 TE S1 по EN 12004, слой 5 мм | аналог: Litokol K80 Eco | | аналог: | кг | 434 | | 18 меш. по 25 кг; 1,5 кг/м² на 1 мм слоя + 10 %; в т. ч. 10 кг — позиции раскладки без марки |
| 23 | Гидроизоляция обмазочная мокрых зон: пол, стены по периметру, зоны замачивания; 2 слоя с армирующей лентой в углах | аналог по характеристикам | | | м² | 16,2 | | площадь по листу раскладки плитки + 10 %; расход смеси — по ТУ |
| 24 | Лента демпферная по периметру пола из плитки | аналог по характеристикам | | | м | 29,1 | | периметр без дверных проёмов + 10 % |

## Примечания

1. Количества — из геометрии проекта: площади поверхностей по чистым граням стен до отделки (те же, что в ведомости отделки и колерной карте), плитка, клей и затирка — по раскладке плиточника; в графе «Кол.» — к заказу, с запасом.
2. Краска: расход 0,12 л/м² на слой в 2 слоя, если по ТУ не задан иной; запас 10 % и 0,5 л на подкраску каждого кода. Один код — одна партия, колеровка машинная в колеровочном центре бренда; в заказ — только после утверждения выкраса (колерная карта). Фасовка — по каталогу бренда на дату выпуска; к заказу — не меньше расчётного объёма.
3. «Аналог по характеристикам» — допускается изделие другого производителя с характеристиками не ниже указанных, по согласованию с автором проекта.
4. Графы «Код продукции» и «Масса 1 ед.» не заполнены: коды по классификатору продукции не присвоены, масса единицы до 25 кг (ГОСТ 21.110-2013).
5. Грунтовка и клей для доски указаны площадью обработки; объём — по ТУ выбранного продукта.

| | | | | |
|---|---|---|---|---|
| | Лист | № док. | Подпись | Дата |
| Дизайнер | Кырлан А.С. | | | 05.10.26 |


Проект: Четырёхкомнатная квартира

Спецификация отделочных материалов

| Стадия | Лист | Листов |
|---|---|---|
| П | С2 | 111 |


## 1 Порог 15 мм: мокрая зона — жилое помещение (М 1:5)

Применение: двери

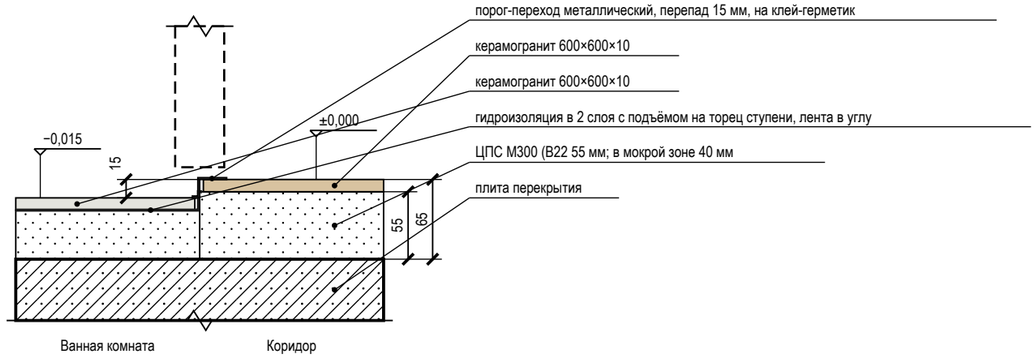



## 2 Стык покрытий пола Т-профилем без перепада (М 1:5)

Применение: проёмы 3↔5, 4↔5, 6↔7, 7↔8, 8↔7, 9↔7

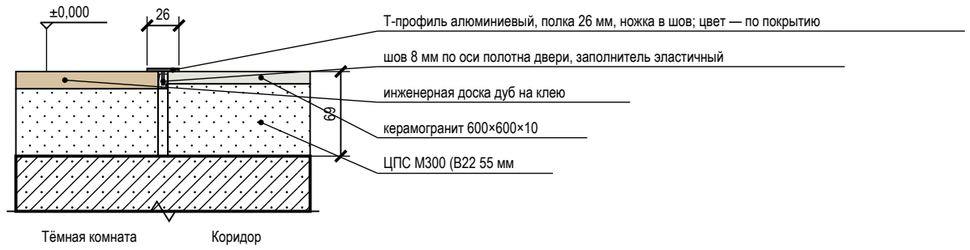



## 3 Короб стояков К1-1, В1-1, Т3-1 с люком и звукоизоляцией (М 1:20)

Применение: пом. 9

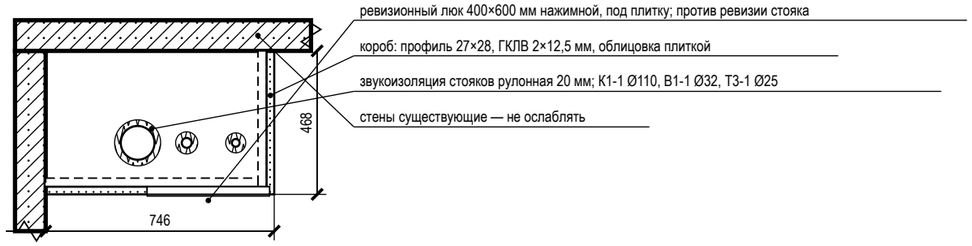



## 4 Гидроизоляция санузла: заход на стены 200 мм, примыкание ванны (М 1:20)

Применение: пом. 2, 10

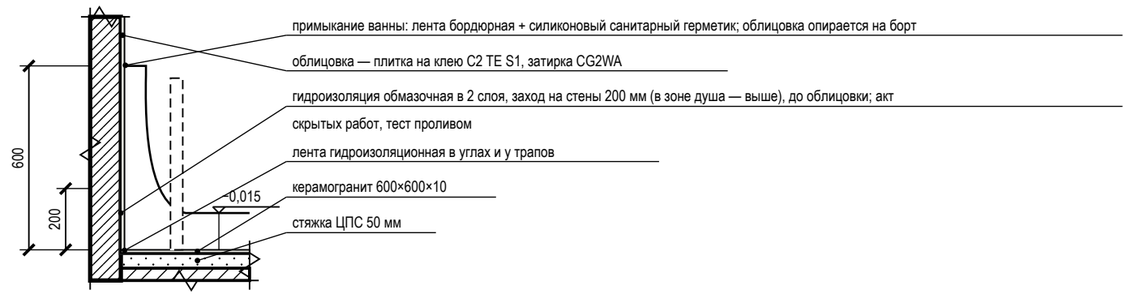


## 5 Плинтус МДФ 80×16 мм у окрашенной стены (М 1:10)

Применение: пом. 1, 3, 4, 5, 6, 7, 8, 9, 11, 12

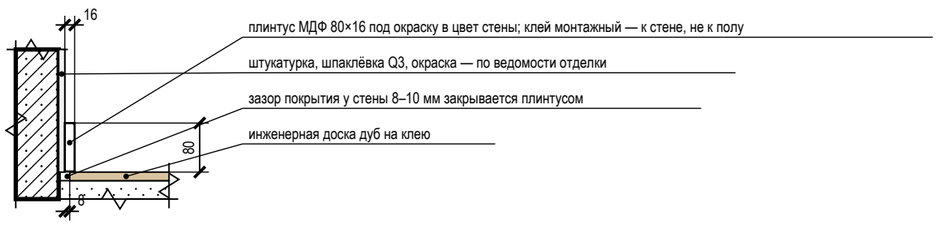


## Условные обозначения

- железобетон (плита, стены)
- кладка, перегородка
- стяжка, раствор
- гипсокартон ГКЛВ
- звукоизоляция, эластичный заполнитель
- плитка, керамогранит на клею
- инженерная доска (покрытие пола)
- металлический профиль (порог, Т-профиль, короб двери)
- гидроизоляция (обмазочная, лента)

## Примечания

1. Узлы — типовые решения проекта для мест, отмеченных выносками на листе схемы расположения развёрток и узлов; размеры — в мм, отметки — в м от ±0,000.
2. Узлы с гидроизоляцией, закладными и коробами скрытого монтажа принимаются по актам скрытых работ до закрытия отделкой; гидроизоляция — после теста проливом (24 ч).
3. Марки изделий (порог, Т-профиль, короб скрытой двери, люк) — по спецификациям; замена — на аналог с теми же габаритами по согласованию с автором проекта.

| | | | | | |
|---|---|---|---|---|---|
| | | | | | Проект: Четырёхкомнатная квартира |
| | Лист | № док. | Подпись | Дата | |
| Дизайнер | Кырлан А.С. | | | 05.10.26 | Узлы |
| | | | | | Стадия: П; Лист: С3; Листов: 111 |

выпуск 05.10.2026 № 05166c8858 · стр. 111 из 111