LINEA

РАБОЧАЯ ДОКУМЕНТАЦИЯ

# Трёхкомнатная квартира

*Warm Contemporary*

Шифр комплекта ГД-2026-003-АИ

Стадия РП

Дата выпуска 05.10.2026

**ПРЕДВАРИТЕЛЬНО · не для производства работ**
**открыто пунктов: 31 (реестр — л. 6–11)**


ДИЗАЙНЕР

**Кырлан Александр Сергеевич**

выпуск 05.10.2026 · 6add39ab8d · стр. 1 из 137

# Содержание

ПРЕДВАРИТЕЛЬНО · не для производства работ · открыто пунктов: 31 (реестр — л. 6–11)

03 Общие данные 20 л.

23 Архитектурные решения 4 л.

28 Планировочное решение 4 л.

33 Электрооборудование 8 л.

42 Отопление и вентиляция 2 л.

45 Водоснабжение и канализация 5 л.

51 Потолки и ГКЛ-конструкции 6 л.

58 Полы и отделка 6 л.

65 Декор и текстиль 11 л.

77 Развёртки и узлы 20 л.

98 Смета 8 л.

107 Визуализации 30 л.



выпуск 05.10.2026 № 6add39ab8d · стр. 2 из 137

ДИЗАЙН-ПРОЕКТ ИНТЕРЬЕРА

# Трёхкомнатная квартира

## *Warm Contemporary*

**78,95 м²**

актуальность · комфорт · мягкая геометрия · контраст фактур · открытость · уверенность

Warm contemporary: потолки V503, стены Skimming Stone No. 241, грейж H487 в текстиле, один глубокий акцент Hague Blue No. 30 (изголовья спален, ТВ-стена).

ПАЛИТРА 60 / 30 / 10

| V503 | F&B No. 241 | H487 | F&B No. 30 |
|---|---|---|---|
| 60 % | 30 % | 10 % | |

B1 · Вид сверху (3D): планировка с мебелью, текстилем и декором

| ОБЪЕКТ | ОБЩАЯ ПЛОЩАДЬ | ПОМЕЩЕНИЙ |
|---|---|---|
| Трёхкомнатная квартира | 78,95 м² | 8, из них жилых 3 |

| СТИЛЬ | СТАДИЯ | ШИФР |
|---|---|---|
| Современный (контемпорари) · warm contemporary | Рабочий проект · предварительно | ГД-2026-003-АИ |

АВТОР ПРОЕКТА

**Кырлан Александр Сергеевич**

Октябрь 2026

| Изм. | Кол.уч | Лист | № док. | Подп. | Дата | ГД-2026-003-АИ | | |
|---|---|---|---|---|---|---|---|---|
| | | | | | | Трёхкомнатная квартира<br>Общая площадь 78,95* м² · * размеры со скана, не замерены (реестр — п. 6–11, К-13) | | |
| Разраб. | | Кырлан А.С. | | | 05.10.26 | Дизайн-проект интерьера трёхкомнатной квартиры | Стадия: РП | Лист: 1 / Листов: 94 |
| Пров. | | | | | | | | |
| ГИП | | | | | | | | |
| Н. контр. | | | | | | Титульный лист<br>М б/м | Кырлан Александр Сергеевич | |
| Утв. | | | | | | | | |

# Общие данные

Комплект ГД-2026-003-АИ · Квартира 3К · Warm Contemporary

Допущения и предложения на листе. Знак «**» предложено (согласовать). См. лист открытых вопросов (листы 6–11).

### Ведомость рабочих чертежей основного комплекта ГД-2026-003-АИ

| Лист | Наименование | Примечание |
|---|---|---|
| 1 | Титульный лист | |
| 2 | Общие данные | |
| 3 | Общие данные | |
| 4 | Общие данные | |
| 5 | Общие данные | |
| 6 | Открытые вопросы, принятые допущения и конфликты. Лист 1 из 6 | |
| 7 | Открытые вопросы, принятые допущения и конфликты. Лист 2 из 6 | |
| 8 | Открытые вопросы, принятые допущения и конфликты. Лист 3 из 6 | |
| 9 | Открытые вопросы, принятые допущения и конфликты. Лист 4 из 6 | |
| 10 | Открытые вопросы, принятые допущения и конфликты. Лист 5 из 6 | |
| 11 | Открытые вопросы, принятые допущения и конфликты. Лист 6 из 6 | |
| 12 | Задание на контрольный обмер и обследование. Лист 1 из 5 | |
| 13 | Задание на контрольный обмер и обследование. Лист 2 из 5 | |
| 14 | Задание на контрольный обмер и обследование. Лист 3 из 5 | |
| 15 | Задание на контрольный обмер и обследование. Лист 4 из 5 | |
| 16 | Задание на контрольный обмер и обследование. Лист 5 из 5 | |
| 17 | График закупок и работ. Лист 1 из 4 | |
| 18 | График закупок и работ. Лист 2 из 4 | |
| 19 | График закупок и работ. Лист 3 из 4 | |
| 20 | График закупок и работ. Лист 4 из 4 | |
| 21 | Обмерный план | |
| 22 | План демонтажа и монтажа перегородок | |
| 23 | Ведомость демонтажа и монтажа перегородок | |
| 24 | План дверей и ведомость заполнения проёмов | |
| 25 | Концепция интерьера | |
| 26 | План расстановки мебели | |
| 27 | Спецификация мебели и оборудования | |
| 28 | Спецификация мебели и оборудования (продолжение) | |
| 29 | План розеток и электровыводов | |
| 30 | План освещения | |

### Ведомость рабочих чертежей основного комплекта ГД-2026-003-АИ (продолжение)

| Лист | Наименование | Примечание |
|---|---|---|
| 31 | План выключателей и схема включения | |
| 32 | Ведомость электроточек и изделий | |
| 33 | Ведомость электроточек и изделий (продолжение) | |
| 34 | Однолинейная схема щита | |
| 35 | План принципиальных трасс | |
| 36 | План слаботочных сетей | |
| 37 | План вентиляции | |
| 38 | План отопления | |
| 39 | План выводов сантехники | |
| 40 | Схема разводки водопровода и канализации | |
| 41 | Спецификация сантехнического оборудования | |
| 42 | Спецификация светильников и сценарии освещения | |
| 43 | Схема каркаса перегородки П-1** | |
| 44 | План потолков | |
| 45 | Разрезы и узлы потолков | |
| 46 | Раскладка плитки. Планы полов | |
| 47 | Раскладка плитки. Прихожая. Фартук кухни | |
| 48 | Раскладка плитки. Ванная. Развёртки стен | |
| 49 | Раскладка плитки. Санузел 2. Развёртки стен | |
| 50 | План полов | |
| 51 | Ведомость отделки помещений | |
| 52 | Колерная карта | |
| 53 | Спецификация отделочных материалов | |

Общие указания — лист 5: ±0,000 — чистый пол; несущие конструкции и сети дома — по отдельному проекту; скрытые работы — по актам. Открытые вопросы и допущения — листы 6–11.

| Изм. | Кол.уч | Лист | № док. | Подп. | Дата | ГД-2026-003-АИ | | |
|---|---|---|---|---|---|---|---|---|
| | | | | | | Трёхкомнатная квартира<br>Общая площадь 78,95* м² · * размеры со скана, не замерены (реестр — п. 6–11, К-13) | | |
| Разраб. | | Кырпан А.С. | | | 05.10.26 | Дизайн-проект интерьера трёхкомнатной квартиры | Стадия: РП | Лист: 2 / Листов: 94 |
| Пров. | | | | | | | | |
| ГИП | | | | | | | | |
| Н. контр. | | | | | | Общие данные<br>М 6/м | Кырпан Александр Сергеевич | |
| Утв. | | | | | | | | |

выпуск 05.10.2026 № 6add39ab8d · стр. 4 из 137

# Общие данные

Комплект ГД-2026-003-АИ · лист 2 общих данных (продолжение)

Допущения и предложения на листе. См. лист открытых вопросов (листы 6–11).

**Ведомость рабочих чертежей основного комплекта ГД-2026-003-АИ (продолжение)**

| Лист | Наименование | Примечание |
|---|---|---|
| 54 | Концепция декора и визуализации | |
| 55 | План текстиля и декора | |
| 56 | Шторы и карнизы | |
| 57 | Ведомость текстиля | |
| 58 | Ведомость декора. Схемы развески | |
| 59 | Встроенная мебель. Схема расположения | |
| 60 | Шкаф распашной С5 | |
| 61 | Система хранения Г1 | |
| 62 | Шкаф-купе М16 | |
| 63 | Кухня (пом. 6). Развёртка гарнитура | |
| 64 | Кухня (пом. 6). Монтажная схема | |
| 65 | Шкафы. Монтажная схема | |
| 66 | Ведомости изделий, техники и фурнитуры | |
| 67 | Реестр марок отделки и позиций альбома | |
| 68 | Схема расположения развёрток и узлов | |
| 69 | Развёртки стен А, Б. Спальня 1 (пом. 1) | |
| 70 | Развёртки стен В, Г. Спальня 1 (пом. 1) | |
| 71 | Развёртки стен А, Б. Ванная (пом. 2) | |
| 72 | Развёртки стен В, Г. Ванная (пом. 2) | |
| 73 | Развёртки стен. Гардеробная (пом. 3) | |
| 74 | Развёртки стен А, Б. Спальня 2 (пом. 4) | |
| 75 | Развёртки стен В, Г. Спальня 2 (пом. 4) | |
| 76 | Развёртки стен А, Б, В. Прихожая (пом. 5) | |
| 77 | Развёртка стены Г. Прихожая (пом. 5) | |
| 78 | Развёртка стены Б2. Кухня-гостиная (пом. 6), кухонный фронт | |
| 79 | Развёртка стены В1. Кухня-гостиная (пом. 6), кухонный фронт | |
| 80 | Развёртки стен А, Б1. Кухня-гостиная (пом. 6) | |
| 81 | Развёртки стен В2, Г1, Г2. Кухня-гостиная (пом. 6) | |
| 82 | Развёртки стен А, Б. Санузел 2 (пом. 7) | |
| 83 | Развёртки стен В, Г. Санузел 2 (пом. 7) | |

Общие указания — лист 5: ±0,000 — чистый пол; несущие конструкции и оси дома — по отдельному проекту; скрытые работы — по актам. Открытые вопросы и допущения — листы 6–11.

**Ведомость рабочих чертежей основного комплекта ГД-2026-003-АИ (продолжение)**

| Лист | Наименование | Примечание |
|---|---|---|
| 84 | Развёртки стен А, Б, В. Коридор (пом. 8) | |
| 85 | Развёртка стены Г. Коридор (пом. 8) | |
| 86 | Узлы | |
| 87 | Ведомость объёмов работ | |
| 88 | Ведомость объёмов работ (продолжение) | |
| 89 | Ведомость объёмов работ (окончание) | |
| 90 | Спецификация материалов | |
| 91 | Спецификация материалов (продолжение) | |
| 92 | Спецификация материалов (окончание) | |
| 93 | Смета ориентировочная | |
| 94 | Смета ориентировочная (окончание) | |

**Ведомость ссылочных и прилагаемых документов**

| Обозначение | Наименование | Примечание |
|---|---|---|
| | Ссылочные документы | |
| ГОСТ 21.201-2011 | СПДС. Условные графические изображения элементов зданий, сооружений и конструкций | |
| ГОСТ 21.205-2016 | СПДС. Условные обозначения элементов санитарно-технических систем | |
| ГОСТ 21.210-2014 | СПДС. Изображения условные графические электрооборудования и проводок на планах | |
| ГОСТ 2.306-68 | ЕСКД. Обозначения графические материалов и правила их нанесения на чертежах | |
| | Прилагаемые документы | |
| ГД-2026-003-АИ.В1 | Визуализация. Вид сверху (3D): планировка с мебелью, текстилем и декором | альбом визуализаций |

| Изм. | Кол.уч | Лист | № док. | Подп. | Дата | ГД-2026-003-АИ | | |
|---|---|---|---|---|---|---|---|---|
| | | | | | | Трёхкомнатная квартира<br>Общая площадь 78,95* м² · * размеры со скана, не замерены (реестр — п. 6–11, К-13) | | |
| Разраб. | | Кырпан А.С. | | | 05.10.26 | Дизайн-проект интерьера трёхкомнатной квартиры | Стадия: РП | Лист: 3 / Листов: 94 |
| Пров. | | | | | | | | |
| ГИП | | | | | | | | |
| Н. контр. | | | | | | Общие данные<br>М 6/м | Кырпан Александр Сергеевич | |
| Утв. | | | | | | | | |

выпуск 05.10.2026 · 6add39ab8d · стр. 5 из 137

# Общие данные

Комплект ГД-2026-003-АИ · лист 3 общих данных (продолжение)

## Ведомость ссылочных и прилагаемых документов (продолжение)

| Обозначение | Наименование | Примечание |
|---|---|---|
| ГД-2026-003-АИ.В2 | Визуализация. Потолок: Ванная (пом. 2) | |
| ГД-2026-003-АИ.В3 | Визуализация. Потолок: Спальня 1 (пом. 1) | |
| ГД-2026-003-АИ.В4 | Визуализация. Потолок: Спальня 2 (пом. 4) | |
| ГД-2026-003-АИ.В5 | Визуализация. Потолок: Прихожая (пом. 5) | |
| ГД-2026-003-АИ.В6 | Визуализация. Потолок: Кухня-гостиная (пом. 6) | |
| ГД-2026-003-АИ.В7 | Визуализация. Потолок | |
| ГД-2026-003-АИ.В8 | Визуализация. Интерьер: Ванная (пом. 2) | |
| ГД-2026-003-АИ.В9 | Визуализация. Визуализация «room-bath1-wB» | |
| ГД-2026-003-АИ.В10 | Визуализация. Визуализация «room-bath1-wC» | |
| ГД-2026-003-АИ.В11 | Визуализация. Визуализация «room-bath1-wD» | |
| ГД-2026-003-АИ.В12 | Визуализация. Визуализация «room-bath2-wB» | |
| ГД-2026-003-АИ.В13 | Визуализация. Визуализация «room-bath2-wC» | |
| ГД-2026-003-АИ.В14 | Визуализация. Интерьер: Спальня 1 (пом. 1) | |
| ГД-2026-003-АИ.В15 | Визуализация. Визуализация «room-bedroom1-wA» | |
| ГД-2026-003-АИ.В16 | Визуализация. Визуализация «room-bedroom1-wB» | |
| ГД-2026-003-АИ.В17 | Визуализация. Интерьер: Спальня 2 (пом. 4) | |
| ГД-2026-003-АИ.В18 | Визуализация. Визуализация «room-bedroom2-wA» | |
| ГД-2026-003-АИ.В19 | Визуализация. Визуализация «room-bedroom2-wD» | |
| ГД-2026-003-АИ.В20 | Визуализация. Визуализация «room-corridor-wA» | |
| ГД-2026-003-АИ.В21 | Визуализация. Визуализация «room-corridor-wC» | |
| ГД-2026-003-АИ.В22 | Визуализация. Интерьер: Прихожая (пом. 5) | |
| ГД-2026-003-АИ.В23 | Визуализация. Визуализация «room-hall-wC» | |
| ГД-2026-003-АИ.В24 | Визуализация. Интерьер: Кухня-гостиная (пом. 6) | |
| ГД-2026-003-АИ.В25 | Визуализация. Интерьер: Кухня-гостиная (пом. 6) | |
| ГД-2026-003-АИ.В26 | Визуализация. Визуализация «room-living-tv» | |
| ГД-2026-003-АИ.В27 | Визуализация. Визуализация «room-living-wB» | |
| ГД-2026-003-АИ.В28 | Визуализация. Визуализация «room-living-wC» | |
| ГД-2026-003-АИ.В29 | Визуализация. Визуализация «room-living-wD» | |
| ГД-2026-003-АИ.В30 | Визуализация. Визуализация «room-wc2» | |

Общие указания — лист 5: ±0,000 — чистый пол; несущие конструкции и сети дома — по отдельному проекту; скрытые работы — по актам. Открытые вопросы и допущения — листы 6–11.

## Состав дизайн-проекта

| Раздел | Состав | Листы |
|---|---|---|
| Обложка | Дизайн-проект интерьера трёхкомнатной квартиры; Трёхкомнатная квартира; автор проекта — Кырлан Александр Сергеевич | 1 с. |
| Концепция | Стиль Современный (контемпорари): концепция интерьера, палитра и материалы (колерная карта — лист 52) | л. 25 |
| Визуализации | 30 изобр.: Вид сверху (3D): планировка с мебелью, текстилем и декором; Потолок: Ванная; Потолок: Спальня 1; Потолок: Спальня 2; Потолок: Прихожая; Потолок: Кухня-гостиная; Потолок; Ванная; Визуализация «room-bath1-wB»; Визуализация «room-bath1-wC»; Визуализация «room-bath1-wD»; Визуализация «room-bath2-wB»; Визуализация «room-bath2-wC»; Спальня 1; Визуализация «room-bedroom1-wA»; Визуализация «room-bedroom1-wB»; Спальня 2; Визуализация «room-bedroom2-wA»; Визуализация «room-bedroom2-wD»; Визуализация «room-corridor-wA»; Визуализация «room-corridor-wC»; Прихожая; Визуализация «room-hall-wC»; Кухня-гостиная; Кухня-гостиная; Визуализация «room-living-tv»; Визуализация «room-living-wB»; Визуализация «room-living-wC»; Визуализация «room-living-wD»; Визуализация «room-wc2» | В1–В30 |
| Рабочие чертежи | планы, развёртки, узлы (развёртки и узлы — листы 68–76, 80–84, 86) | л. 1–94 |
| Спецификации и ведомости | оборудование, изделия, отделка, электроточки | л. 23, 24, 27, 28, 32, 33, 41, 42, 51–53, 57, 58, 87–92 |

**Допущения и предложения на листе**

Основа листа: размеры сняты со скана плана заказчика по размерным цепочкам, контрольный обмер на объекте не выполнялся (К-13); высота потолка 2700 мм принята: на плане заказчика не указана (К-11); толщины стен приняты: наружные 250 мм, перегородки 150 мм (на плане 85–190 мм) (К-13); разрешённая мощность 15 кВт принята по типовой квартире, технических условий нет (К-14); утолщение стены 190 × 1360 мм и элемент 1470 × 160 мм плана заказчика не определены (К-12); ниши санузла 2 закрыты перегородкой и фальш-стеной: проектное решение, на плане заказчика ниша у входа открыта (К-18); несущие стены не определены: до технического заключения все существующие стены считаются несущими (К-20); окна существующие и сохраняются; подоконная доска и глубина откосов не заданы — приняты, не замерены (К-27).

См. лист открытых вопросов (лист 6, запись К-11; лист 7, записи К-12–К-14, К-18, К-20; лист 8, запись К-27).

| Изм. | Кол.уч | Лист | № док. | Подп. | Дата |
|---|---|---|---|---|---|
| Разраб. | | Кырлан А.С. | | | 05.10.26 |
| Пров. | | | | | |
| ГИП | | | | | |
| | | | | | |
| Н. контр. | | | | | |
| Утв. | | | | | |

**ГД-2026-003-АИ**

Трёхкомнатная квартира

Общая площадь 78,95* м² · * размеры со скана, не замерены (реестр — л. 6–11, К-13)

| Дизайн-проект интерьера трёхкомнатной квартиры | Стадия | Лист | Листов |
|---|---|---|---|
| | РП | 4 | 94 |
| **Общие данные** М 6/м | Кырлан Александр Сергеевич | | |

выпуск 05.10.2026 ⚲ 6add39ab8d · стр. 6 из 137

# Общие данные

Комплект ГД-2026-003-АИ · лист 4 общих данных (продолжение)

## Условные обозначения

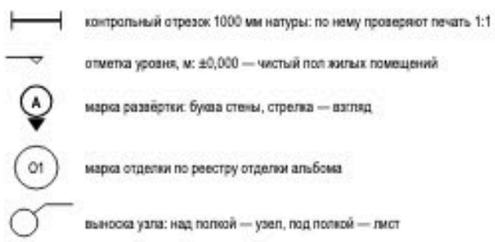


контрольный отрезок 1000 мм натуры: по нему проверяют печать 1:1

отметка уровня, м: ±0,000 — чистый пол жилых помещений

марка развёртки: буква стены, стрелка — взгляд

марка отделки по реестру отделки альбома

выноска узла: над полкой — узел, под полкой — лист

## Общие указания

1. Рабочие чертежи интерьера разработаны на основании задания на проектирование и обмерного плана (лист 21). Объект: Трёхкомнатная квартира; автор проекта — Кырлан Александр Сергеевич; общая площадь 78,95 м², жилая 59,75 м², помещений 8.
2. Рабочие чертежи выполнены в соответствии с заданием на проектирование и нормативными документами, перечисленными в п. 4.
3. Открытые вопросы, принятые допущения и конфликты между разделами, не снятые к выпуску комплекта, сведены в таблицы на листах 6–11. До ответа по пункту таблицы показанное на указанном там листе — допущение, а не утверждённое решение: комплект по этим листам предварительный.
4. Нормативные документы, на которые есть ссылки в листах комплекта: ГОСТ Р 21.101-2026; ГОСТ 21.501-2018; ГОСТ 2.302-68; ГОСТ 2.303-68; ГОСТ 2.304-81; ГОСТ 2.307-2011; СП 54.13330.2022; СП 71.13330.2017; СП 73.13330.2016; ПУЭ (7-е изд.), гл. 1.8, 7.1; ГОСТ Р 50571.7.701-2024; СанПиН 1.2.3685-21; ГОСТ 2.702; ГОСТ 2.755; ГОСТ 21.110-2013; ГОСТ 21.601; ГОСТ 13996-2019; ГОСТ 31565-2012; ГОСТ 31975; ГОСТ 32414-2013; ГОСТ 32415-2013; ГОСТ 32614-2012; ГОСТ Р 56387-2018; СП 29.13330.2011; СП 30.13330.2020; СП 51.13330.2011; СП 52.13330.2016. Документы из ведомости ссылочных документов здесь не повторяются.
5. За отметку ±0,000 принят уровень чистого пола жилых помещений квартиры (относительная отметка; абсолютная — по проекту дома). Отметка чистого пола мокрых помещений — −0,015. Размеры — в миллиметрах, отметки — в метрах, площади — в м²; высоты установки Н от чистого пола своего помещения до оси изделия.
6. Несущие конструкции, общедомовые стояки, вентиляционные каналы и инженерные сети дома настоящим комплектом не изменяются. Работы, затрагивающие их (проём или штраба в несущей стене, перенос стояка, врезка в вентканал, расширение мокрой зоны), выполняются только по отдельному проекту, к которому прилагается техническое заключение о допустимости и безопасности работ, выданное автором проекта дома или организацией с допуском на обследование, и который согласован в установленном порядке (Жилищный кодекс РФ, ст. 25–29).
7. Трассы инженерных сетей на листах — принципиальные. Расчёты электрических нагрузок и токов КЗ, гидравлики, воздухообмена, освещённости и нагрузок на перекрытие выполняются в проектах ЭОМ, ВК, ОВ и КР организацией с допуском СРО; фактические трассы до закрытия отделкой фиксируются исполнительными схемами.
8. Стиль интерьера — Современный (контемпорари). Палитра проекта: основной 60 % — Tikkurila V503 «Winter», Farrow & Ball No. 241 «Skimming Stone»; дополнительный 30 % — Tikkurila H487 «Pumice»; акцент 10 % — Farrow & Ball No. 30 «Hague Blue». Коды цвета — по веерам производителей; цвет утверждается по выкрасу на объекте при освещении проекта.
9. Площади поверхностей — по чистым граням стен до отделки: стены = периметр × высоту от чистого пола помещения до низа потолка минус проёмы (облицовка плиткой — до верха облицовки); плинтус = периметр минус дверные проёмы; пол и потолок — по площади помещения. Количество плиток — по раскладке. Способ один для всех листов комплекта (ведомость отделки, коперная карта, раскладка плитки, развёртки).
10. Марки: стены помещения на всех листах — А (верхняя по плану), Б (правая), В (нижняя), Г (левая); марка отделки О — одна на весь альбом; реестр марок отделки (с позициями коперной карты той же отделки) и марки позиций по видам — на листе 67.
11. Развёртки стен выполнены по всем помещениям для стен с электроточками, мебелью, декором и отделкой: санузлы и кухонный фронт — в М 1:25, остальные стены — в М 1:40; расположение развёрток и узлов — на листе 68, узлы — на листе 86.
12. Перечень скрытых работ, на которые составляются акты освидетельствования (форма по приказу Минстроя России № 344/пр): гидроизоляция пола и стен мокрых помещений (с тестом проливом); стяжка пола (толщина, прочность, влажность основания); скрытая электропроводка (за потолком и в штробах стен; условия штробления — в следующем пункте); трубопроводы водоснабжения и канализации до закрытия (опрессовка, уклоны); закладные и усиления под подвесные приборы, мебель и тяжёлый декор, рамы инсталляций; короба дверей скрытого монтажа до штукатурки; каркасы ГКЛ потолков, коробов и перегородок до обшивки.
13. Скрытая электропроводка: за потолком и в штробах стен. Штробы в стенах выполняются только после технического заключения о несущих конструкциях; до заключения несущие стены не определены, и все стены считаются несущими; объём штроб — в ведомости объёмов работ, строка «Штробы в стенах» (вертикальные спуски; объём не меньше фактического, горизонтальные трассы — по исполнительной схеме).
14. Критерии приёмки: допуски отделочных покрытий — по СП 71.13330.2017; испытания систем водоснабжения и канализации — по СП 73.13330.2016 до закрытия трасс; приёмо-сдаточные испытания электроустановки — по ПУЭ, гл. 1.8, с протоколом электролаборатории.
15. Осознанные отступления от ГОСТ Р 21.101-2026, принятые в комплекте: номер листа и число листов («Листов») указаны на каждом листе; на масштабных листах в основной надписи указан фактический масштаб и дан контрольный отрезок 1000 мм; развёртки стен выполнены в М 1:25 и 1:40 (ГОСТ 21.507-81 — 1:50…1:500) ради читаемости привязок; размерные числа и марки элементов (Д-1, ОК-1, О6) — кеглем 2,5 мм, номера помещений — в кружке Ø 8 мм (канон — 3,5 мм и Ø 12 мм): так насыщенные листы А3 читаются без наложений надписей.
16. Графы «Пров.», «Н. контр.», «Утв.» основной надписи заполняются при согласовании комплекта с заказчиком; до согласования комплект подписывает автор проекта (графа «Разраб.»).

**Допущения и предложения на листе**

Основа листа: размеры сняты со скана плана заказчика по размерным цепочкам, контрольный обмер на объекте не выполнялся (К-13); высота потолка 2700 мм принята: на плане заказчика не указана (К-11); толщины стен приняты: наружные 250 мм, перегородки 150 мм (на плане 85–190 мм) (К-13); разрешённая мощность 15 кВт принята по типовой квартире, технических условий нет (К-14); утолщение стены 190 × 1360 мм и элемент 1470 × 160 мм плана заказчика не определены (К-12); ниши санузла 2 закрыты перегородкой и фальш-стеной: проектное решение, на плане заказчика ниша у входа открыта (К-18); несущие стены не определены: до технического заключения все существующие стены считаются несущими (К-20); окна существующие и сохраняются; подоконная доска и глубина откосов не заданы — приняты, не замерены (К-27).

См. лист открытых вопросов (лист 6, запись К-11; лист 7, записи К-12–К-14, К-18, К-20; лист 8, запись К-27).

| | | | | | | | | |
|---|---|---|---|---|---|---|---|---|
| | | | | | | **ГД-2026-003-АИ** | | |
| | | | | | | Трёхкомнатная квартира | | |
| | | | | | | Общая площадь 78,95* м² · * размеры со скана, не замерены (реестр — п. 6–11, К-13) | | |
| Изм. | Кол.уч | Лист | № док. | Подп. | Дата | | | |
| Разраб. | | Кырлан А.С. | | | 05.10.26 | Дизайн-проект интерьера трёхкомнатной квартиры | Стадия | Лист | Листов |
| Пров. | | | | | | | РП | 5 | 94 |
| ГИП | | | | | | | | | |
| | | | | | | **Общие данные** | Кырлан Александр Сергеевич | | |
| Н. контр. | | | | | | М 6/м | | | |
| Утв. | | | | | | | | | |

выпуск 05.10.2026 № 6add39ab8d · стр. 7 из 137

# Открытые вопросы, принятые допущения и конфликты. Лист 1 из 6

Сводка по реестрам координации

Комплект предварительный по пунктам этих таблиц. Пока по пункту нет ответа или решения, показанное на указанном листе — допущение проектировщика, а не утверждённое решение.
Сводка: открытых вопросов — 26 (из них ждут факта объекта — 16: контрольного обмера, обследования или документа); изменений в реестре — 17, из них без подписи — 5.
Пункты, ответ на которые лежит на объекте, а не за столом проектировщика (графа «Вид», строка «Ждёт»), собраны на листе «Задание на контрольный обмер и обследование» (листы 12–16): что и где замерить, с какой точностью и чем подтвердить. Пункты, ждущие решения человека, на объекте не закрываются.

## Открытые вопросы и принятые допущения

| № | Формулировка | Вид | Кто решает | Если решения нет | Лист, где это проявляется |
|---|---|---|---|---|---|
| К-1 | Ванная (2250 × 1970 мм): после утверждения стиральной машины с вертикальной загрузкой 400 × 600 мм (ИЗ-11) замечания по дверце машины и боковому зазору унитаза П2 сняты. Остаются: в зоне 750 мм перед ванной П1 стоит умывальник П3; розетка Р7 в 348 мм от стояка (нужно 500). Предложение, в проект не принято: умывальник П3 развернуть до 600 × 450 мм к стене В, унитаз П2 сдвинуть на 150 мм, розетки Р7 и Р8, светильник и зеркало перенести по новой раскладке. Решить: принять предложение, оставить как есть с открытыми замечаниями или предложить другую раскладку. | Спорно<br>Ждёт: решения | Инженер ВК (вода, канализация) | в проекте остаются умывальник П3 в зоне перед ванной и розетка Р7 в 348 мм от стояка; эти отступления остаются открытыми | л. 39 — План выводов сантехники<br>л. 29 — План розеток и электровыводов |
| К-2 | Артикул плитки и калибр партии (фактический размер плитки) для ванной и санузла 2 не заданы: раскладка рассчитана по номинальным размерам — пол 600 × 600 мм, стены 600 × 1200 мм. Требование к закупке: выбрать плитку и до раскладки измерить калибр на образце партии (или взять из паспорта партии); раскладку пересчитать по измеренному калибру до заказа плитки и до укладки. Пока калибр не измерен, подрезка у стен и число плиток по листам раскладки — расчётные. | Отсутствует<br>Ждёт: данных закупки, затем решения | Плиточник | раскладка остаётся по номинальным размерам; подрезку у стен определять по фактической партии, раскладку пересчитать по измеренному калибру | л. 46 — Раскладка плитки. Планы полов<br>л. 48 — Раскладка плитки. Ванная. Развёртки стен<br>л. 49 — Раскладка плитки. Санузел 2. Развёртки стен |
| К-3 | Доли цвета по поверхностям не укладываются в схему 60/30/10 и её варианты: ведущий цвет занимает 33 % в спальне 1, 38 % в спальне 2 и 32 % в кухне-гостиной (нужно от 50 %); акцент в спальне 1 — 19 %, в спальне 2 — 18 % (больше 15 %); в гардеробной ведущий цвет занимает 90 % (больше 80 %), второй цвет почти не читается. Решить, какие поверхности считать ведущим цветом в каждой комнате, или принять распределение как есть. | Спорно<br>Ждёт: решения | Колорист-комплектатор | цвета остаются в показанных долях, ведущий цвет в трёх комнатах не определён | л. 52 — Колерная карта |
| К-4 | Вход в санузел 2 (с унитазом) — из кухни-гостиной: так по плану заказчика (ниша у входа на плане открыта в кухню-гостиную, в проекте закрыта перегородкой по линии низа прихожей). Вход в помещение с унитазом принято устраивать из коридора или прихожей. Принять существующее положение или перепланировать вход. | Спорно<br>Ждёт: решения | Архитектор-планировщик | Остаётся вариант, показанный на листе; он не утверждён, лист предварительный. | л. 21 — Обмерный план<br>л. 24 — План дверей и ведомость заполнения проёмов |
| К-5 | Санузел 2 (1675 × 1580 мм): перед душем П6 до противоположной стены 630 мм (нужно 750); зону перед унитазом П7 и умывальником П8 занимает сам поддон душа П6; боковой зазор умывальника П8 — 150 мм (нужно 200). Принять как проектное решение «перекрытие зон движения» нельзя: VDI 6000 допускает перекрытие зон движения соседних приборов, но не прибор в зоне движения другого, а здесь в зоне стоит поддон душа, и глубина перед душем меньше 750 мм. Отступление от этой зарубежной рекомендации (в российских нормах размеры перед приборами не заданы) возможно только как осознанный отказ от неё при малом помещении либо перестановкой приборов. | Спорно<br>Ждёт: решения | Инженер ВК (вода, канализация) | приборы остаются как показаны: поддон душа стоит в зоне перед унитазом и умывальником, глубина перед душем 630 мм; отступление не принято и не обосновано | л. 39 — План выводов сантехники |
| К-7 | Розетки выше 1 м от пола (норма ПУЭ, п. 6.6.30 — не выше 1 м). Р7 (стиральная машина) и Р8 (фен) в ванной стояли на 1200 мм, Р33 (фен, санузел 2) — на 1100 мм: назначение не требует такой высоты, розетки опущены до 1000 мм (запись ИЗ-9). Остаются выше 1 м по назначению, основание записано в самой позиции (знак «**» у марки, примечание листа, графа «Назначение» ведомости): Р12 (ТВ над комодом, спальня 2) — 1100 мм, питание телевизора на стене, в одной зоне с ТВ2 и LAN2; Р18 (ТВ) и Р19 (ТВ-приставка, кухня-гостиная) — 1100 мм, в одной зоне с ТВ1 и LAN3; Р17 (питание слаботочного щита ЩС, прихожая) — 1700 мм, рядом со щитом на его высоте; Р25 (холодильник) — 2000 мм, над нишей М6 за съёмной панелью. Подтвердить высоты или опустить розетки. | Спорно<br>Ждёт: решения | Инженер-электрик | высоты остаются как на листе, решение не подтверждено | л. 29 — План розеток и электровыводов<br>л. 32, 33 — Ведомость электроточек и изделий |
| К-8 | Проект кухни не утверждён заказчиком: выводы кухонной техники (мойка М7, посудомоечная М14, варочная панель и духовой шкаф М8, вытяжка М15, холодильник М6) приняты по типовой расстановке техники. Раскладка гарнитура принята автором проектной (ИЗ-12) с условием: до начала черновых работ сверить её и выводы техники с чертежом кухни от изготовителя гарнитура; чертёж изготовителя нужно получить и передать. Пока чертежа нет, привязки выводов даны от осей модулей гарнитура и пересматриваются вместе с проектом кухни. | Отсутствует<br>Ждёт: документа, обмера, затем решения | Мебельщик | выводы остаются привязанными к раскладке гарнитура, принятой проектной и не сверенной с чертежом изготовителя | л. 63 — Кухня (пом. 6). Развёртка гарнитура<br>л. 29 — План розеток и электровыводов |
| К-9 | Гардеробная состоит из двух частей; проход между ними через стык — 280 мм (нужно 700 мм), он сужает систему хранения Г1. Принять как технический проход нельзя: по практике проектирования технический проход не уже 700 мм, меньше 600 мм — критично, а 280 мм — уже ширины плеч. Изменить границу частей либо состав Г1. | Спорно<br>Ждёт: решения | Дизайнер интерьера | проход через стык остаётся 280 мм: в часть гардеробной не пройти, пока не изменены граница частей или состав Г1 | л. 26 — План расстановки мебели<br>л. 61 — Система хранения Г1 |
| К-11 | Высота потолка 2700 мм принята: на плане заказчика она не указана. От неё зависят вертикальные размеры альбома (развёртки, шкафы, плитка, объёмы работ). Замерить высоту на объекте. | Непонятно<br>Ждёт: обмера | Архитектор-планировщик | Остаётся значение, принятое по исходным данным; оно не подтверждено, лист предварительный. | л. 21 — Обмерный план |

| | | | | | | | |
|---|---|---|---|---|---|---|---|
| | | | | | | ГД-2026-003-АИ | |
| | | | | | | Трёхкомнатная квартира | |
| | | | | | | Общая площадь 78,95* м² · * размеры со скана, не замерены (реестр — п. 6–11, К-13) | |
| Изм. | Кол.уч | Лист | № док. | Подп. | Дата | Дизайн-проект интерьера трёхкомнатной квартиры | Стадия: РП; Лист: 6; Листов: 94 |
| Разраб. | | Кырпан А.С. | | | 05.10.26 | | |
| Пров. | | | | | | Открытые вопросы, принятые допущения и конфликты. Лист 1 из 6<br>М 6/м | Кырпан Александр Сергеевич |
| ГИП | | | | | | | |
| Н. контр. | | | | | | | |
| Утв. | | | | | | | |

выпуск 05.10.2026 № 6add39ab8d · стр. 8 из 137

# Открытые вопросы, принятые допущения и конфликты. Лист 2 из 6

Сводка по реестрам координации

## Открытые вопросы и принятые допущения (продолжение)

| № | Формулировка | Вид | Кто решает | Если решения нет | Лист, где это проявляется |
|---|---|---|---|---|---|
| К-12 | Две конструкции плана заказчика не определены: утолщение стены 190 × 1360 мм в гардеробной у спальни 2 (вентблок или пилон) и элемент 1470 × 160 мм на линии простенка кухни-гостиной (пилон, балка или барная стойка). Элемент 1470 × 160 мм на листах не показан, мебель от него свободна. Назначение определить на объекте. | Непонятно<br>Ждёт: обследования | Архитектор-планировщик | Остаётся значение, принятое по исходным данным; оно не подтверждено, лист предварительный. | л. 21 — Обмерный план<br>л. 26 — План расстановки мебели |
| К-13 | Размеры сняты со скана плана заказчика по размерным цепочкам, контрольный обмер на объекте не выполнялся; толщины стен приняты 250 мм (наружные) и 150 мм (перегородки), на плане 85–190 мм. В двух местах принятое значение отличается от числа на плане: ширина гардеробной 1070 мм (на плане 1120 при перегородке 85 мм), ширина спальни 2 — 3130 мм (на плане 3120). Привязка стены прихожей к спальне 1 сдвинута на 40 мм относительно плана: на плане толщина стены 190 мм, в модели 150 мм (чистые размеры помещений — по плану, разница отнесена к толщинам стен). Подтвердить контрольным обмером. | Непонятно<br>Ждёт: обмера | Архитектор-планировщик | Остаётся значение, принятое по исходным данным; оно не подтверждено, лист предварительный. | л. 21 — Обмерный план |
| К-14 | Разрешённая мощность 15 кВт принята по типовой квартире, технических условий в материалах объекта нет; расчётная мощность 11,8 кВт. Сверить с техническими условиями. | Непонятно<br>Ждёт: документа | Инженер-электрик | Остаётся значение, принятое по исходным данным; оно не подтверждено, лист предварительный. | л. 34 — Однолинейная схема щита |
| К-15 | Графы «Пров.» и «Н. контр.» в штампе пусты: их заполняет человек, подписи проверяющего и нормоконтролёра разработчик проекта не ставит; для выдачи нужны подписанты, отличные от разработчика. Решение автора (ИЗ-13): графы остаются пустыми, комплект предварительный. | Отсутствует<br>Ждёт: решения | Нормоконтролёр | графы остаются пустыми; комплект предварительный, не проверен независимо | л. 2 — Общие данные |
| К-16 | Сдача разделов специалистами для этого проекта не оформлена (нет файлов решений по ролям). В альбоме нет листов «Пожарная безопасность» и «Звукоизоляция», программы испытаний и приёмки, допуска ГИПа. Решить, какие из этих разделов входят в состав работ; для входящих оформить сдачу. | Отсутствует<br>Ждёт: решения | Главный инженер проекта (ГИП) | Исходных данных нет: на листе нет решения по этому пункту или оно условное; лист предварительный. | л. 2 — Общие данные |
| К-17 | Положение стояков условно, на объекте не замерено: стояки канализации и холодной воды — в коробе Ш1 248 × 459 в углу ванной и в стене-пилоне Ш2 270 мм между санузлом 2 и кухней (по плану заказчика). От положения стояков зависят привязки выводов воды и канализации, расстояния розеток до стояка (К-1) и места люков 300 × 400. Сверить положение стояков на объекте до разметки. | Непонятно<br>Ждёт: обмера | Инженер ВК (вода, канализация) | Остаётся значение, принятое по исходным данным; оно не подтверждено, лист предварительный. | л. 39 — План выводов сантехники<br>л. 40 — Схема разводки водопровода и канализации |
| К-18 | Санузел 2: ниша 1600 × 1840 мм у входа закрыта перегородкой, ниша 660 × 260 мм (уступ по плану) — фальш-стенкой с рамой инсталляции: проектное решение, на плане заказчика ниша у входа открыта в кухню-гостиную. От закрытия зависят размеры санузла 2 (1675 × 1580 мм), перегородка и фальш-стена в объёмах работ. Подтвердить закрытие ниш или оставить их открытыми. | Спорно<br>Ждёт: решения | Архитектор-планировщик | Остаётся вариант, показанный на листе; он не утверждён, лист предварительный. | л. 39 — План выводов сантехники |
| К-19 | Модель стиральной машины П4 не выбрана. Условие закупки (решение автора проекта, ИЗ-11): вертикальная загрузка, габарит в плане 400 × 600 мм (ширина 400 мм вдоль стены Б, глубина 600 мм), высота по паспорту (в расчёте 900 мм). Машина с фронтальной загрузкой или большего габарита проекту не подходит: перед люком ванна П1, дверца не откроется. Тип загрузки и габарит до заказа сверить с паспортом выбранной модели, положение подводов — до закрытия трасс и разводки. В спецификации мебели и оборудования тот же габарит выведен по осям плана как 600 × 400 мм. | Отсутствует<br>Ждёт: данных закупки, затем решения | Инженер ВК (вода, канализация) | машина не куплена: тип загрузки и габарит на листах условие закупки; купленная машина другого типа или габарита потребует пересмотра раскладки ванной | л. 39 — План выводов сантехники<br>л. 41 — Спецификация сантехнического оборудования |
| К-20 | Несущие стены не определены: проект дома и план БТИ в материалах объекта отсутствуют, тип и серия дома неизвестны, техническое заключение о несущих конструкциях не выполнялось. До заключения все существующие стены считаются несущими: демонтаж, новые проёмы и штробы в них не планируются. Нужно: запросить проект дома и поэтажный план БТИ, установить серию дома; несущие стены и допустимость вмешательства определяет техническое заключение специализированной организации. | Отсутствует<br>Ждёт: документа, обследования | Архитектор-планировщик | Исходных данных нет: на листе нет решения по этому пункту или оно условное; лист предварительный. | л. 22 — План демонтажа и монтажа перегородок |
| К-21 | Прямые углы помещений с кухней, санузлами, гардеробной и встроенной мебелью по скану не подтверждены: спальня 1, ванная, гардеробная, прихожая, кухня-гостиная, санузел 2. Нужен контрольный обмер: длины сторон и обе диагонали каждого помещения, отклонения углов от 90° у стен под встроенную мебель и плитку. Только после обмера в данных отмечаются прямые углы. | Отсутствует<br>Ждёт: обмера | Архитектор-планировщик | углы принимаются прямыми по скану, не проверенными; встроенную мебель и плитку по размерам листов не заказывать до обмера | л. 21 — Обмерный план<br>л. 26 — План расстановки мебели |
| К-22 | Состав подрядчиков и поставщиков (кто покупает и кто монтирует радиаторы, подоконники, двери, розетки) от заказчика не получен. Принята типовая схема частного ремонта (ИЗ-14): материалы и оборудование покупает заказчик по спецификациям проекта, монтаж ведёт подрядная бригада, приёмку скрытых работ ведёт автор. Схема уточняется договором подряда: нужен договор или состав подрядчиков и поставщиков от заказчика. | Отсутствует<br>Ждёт: решения | Прораб-координатор | остаётся типовая схема: покупает заказчик, монтирует подрядная бригада, скрытые работы принимает автор; закрепление за конкретными подрядчиками не подтверждено | л. 2 — Общие данные |

| | | | | | | | |
|---|---|---|---|---|---|---|---|
| | | | | | | ГД-2026-003-АИ | |
| | | | | | | Трёхкомнатная квартира | |
| Изм. | Кол.уч | Лист | № док. | Подп. | Дата | Общая площадь 78,95* м² · * размеры со скана, не замерены (реестр — л. 6–11, К-13) | |
| Разраб. | | Кырпан А.С. | | | 05.10.26 | Дизайн-проект интерьера трёхкомнатной квартиры | Стадия: РП; Лист: 7; Листов: 94 |
| Пров. | | | | | | | |
| ГИП | | | | | | | |
| | | | | | | Открытые вопросы, принятые допущения и конфликты. Лист 2 из 6<br>М 6/м | Кырпан Александр Сергеевич |
| Н. контр. | | | | | | | |
| Утв. | | | | | | | |

выпуск 05.10.2026 · 6add39ab8d · стр. 9 из 137

# Открытые вопросы, принятые допущения и конфликты. Лист 3 из 6

Сводка по реестрам координации

## Открытые вопросы и принятые допущения (продолжение)

| № | Формулировка | Вид | Кто решает | Если решения нет | Лист, где это проявляется |
|---|---|---|---|---|---|
| К-23 | Артикулы изделий отделки не выбраны. Инженерная доска (пом. 1, 3, 4, 6, 8), керамогранит пола (пом. 2, 5, 7), керамогранит стен (пом. 2, 7), керамогранит фартука кухни (пом. 6) и плинтус МДФ (пом. 1, 3, 4, 5, 6, 8) заданы характеристиками — «аналог по характеристикам», кода изделия производителя нет. Артикул выбирается при закупке: выбрать изделия, вписать артикулы в ведомость отделки и спецификации, цвет и тон принять по образцу из партии. Количество к заказу и упаковки — расчётные, по номинальным размерам, до выбора изделия. Калибр партии плитки для ванной и санузла 2 — отдельный вопрос К-2. | Отсутствует<br>Ждёт: данных закупки, затем решения | Отделочник | материалы остаются описанными характеристиками; заказ по спецификации и подсчёт упаковок — только после выбора изделий | л. 46 — Раскладка плитки. Планы полов<br>л. 47 — Раскладка плитки. Прихожая. Фартук кухни<br>л. 48 — Раскладка плитки. Ванная. Развёртки стен<br>л. 49 — Раскладка плитки. Санузел 2. Развёртки стен<br>л. 50 — План полов<br>л. 51 — Ведомость отделки помещений<br>л. 53 — Спецификация отделочных материалов<br>л. 67 — Реестр марок отделки и позиций альбома<br>л. 90–92 — Спецификация материалов<br>л. 93, 94 — Смета ориентировочная |
| К-24 | Модели встраиваемой техники кухни не выбраны: холодильник (М6) и посудомоечная машина (М14) заданы описанием «аналог по характеристикам» — без производителя, серии и кода. Размеры ниш и вентзазоры взяты по типовой схеме на 60 см, а не по паспорту модели: у разных изготовителей они расходятся, и модуль, сделанный по типовой нише, может не принять выбранную технику. Нужно: выбрать модели, получить монтажные схемы изготовителей и сверить ниши модулей, вентиляцию и подключение до заказа гарнитура. Вытяжка М15 не встроена (подключение по паспорту изготовителя), но модель тоже не выбрана — выбирается вместе с остальной техникой. Проект кухни целиком — К-8. | Отсутствует<br>Ждёт: данных закупки, затем решения | Мебельщик | ниши остаются по типовой схеме на 60 см, не подтверждённой паспортом модели; модули кухни не заказывать до выбора техники | л. 63 — Кухня (пом. 6). Развёртка гарнитура<br>л. 64 — Кухня (пом. 6). Монтажная схема |
| К-25 | Скрытые двери Д-2 (спальня 1 и спальня 2), Д-3 (ванная) и Д-4 (гардеробная) заданы размером проёма 800×2100 со скана плана заказчика; проёмы существующие, расширять их до технического заключения (К-20) нельзя. Скрытый блок ставят в проём с зазором 10–15 мм на сторону, а коробка занимает часть ширины, поэтому полотно получается уже проёма; размеры короба и полотна задаёт изготовитель, модель не выбрана. У Д-3 и Д-4 принятая толщина стены 150 мм, по скану плана заказчика стена 85 мм: узел скрытой двери на листе узлов показан для принятой толщины 150 мм; по замеренной толщине его пересчитать. Порядок работ один: проём замеряют в чистоте после снятия отделки, короб ставят до штукатурки, полотно навешивают после чистовой отделки стен. Дверь Д-5 стоит в проектной перегородке П-1 (К-18): её проём 700 мм принят проектом, привязка к углу 50 мм; размер короба и полотна — по выбранной модели. Нужно: замерить проёмы и толщину стены в чистоте; решить, делать полотно под существующий проём (уже проёма) или расширять проём после технического заключения; выбрать модель блока и получить размеры короба. | Непонятно<br>Ждёт: обмера, затем решения | Архитектор-планировщик | скрытые двери не заказывать (изготовление около 30 дней): размеры короба и полотна не определены, проёмы не расширять до технического заключения; узел показан для принятой толщины стены 150 мм | л. 24 — План дверей и ведомость заполнения проёмов<br>л. 86 — Узлы |
| К-26 | Входная дверь Д-1 существующая. По плану заказчика полотно открывается наружу, в общий коридор: на плане дверей и обмерном плане дуга показана наружу, как в данных объекта. Направление открывания на объекте не проверено и не выбирается за столом. Не решено, остаётся ли существующий блок или он заменяется: в ведомости объёмов работ заложена строка «Входная дверь, поставка с монтажом и откосами». Нужно: осмотр входной двери (сторона открывания, петли, коробка, откосы) и решение автора оставить блок или заменить, и с каким открыванием. | Непонятно<br>Ждёт: обследования, затем решения | Архитектор-планировщик | на листах дверь показана как в данных объекта (открывание наружу, существующий проём); блок для заказа не определён | л. 24 — План дверей и ведомость заполнения проёмов |
| К-27 | Окна ОК-1…ОК-4 в проекте существующие: демонтажа и замены окон нет ни на плане демонтажа, ни в ведомости объёмов работ; ведомость заполнения проёмов фиксирует их размеры, а не заказ новых блоков. Подоконная доска и глубина откоса не заданы: откосы считаются по умолчанию (толщина стены минус коробка 70 мм), подоконники в проекте не показаны; состояние окон и подоконников не обследовано. Нужно: осмотр окон и решение — окна и подоконники остаются существующими или заменяются. | Непонятно<br>Ждёт: обмера, затем решения | Архитектор-планировщик | окна показаны существующими, заказ оконных блоков не предусмотрен; подоконники и глубина откосов приняты, не замерены | л. 24 — План дверей и ведомость заполнения проёмов |
| К-28 | Сроки поставки и изготовления изделий с длинной поставкой не получены ни от одного поставщика: скрытые двери Д-2…Д-5, кухонный гарнитур, встраиваемая техника, керамогранит, инженерная доска, сантехника и инсталляции, встроенная мебель по замеру цеха. В данных нет срока (leadDays) ни у одной позиции. Типовые диапазоны практики — скрытые двери около 30 дней, кухня и корпусная мебель 4–8 недель от замера — это ориентир, а не срок поставщика: заказывать и назначать даты по ним нельзя. Нужно: запросить у поставщиков и изготовителей срок по выбранным моделям и записать его в данные позиции. | Отсутствует<br>Ждёт: данных закупки, затем решения | Прораб-координатор | график закупок остаётся относительным: порядок и условия есть, дат заказа нет; заказ по типовым срокам не назначается | л. 17–20 — График закупок и работ<br>л. 93, 94 — Смета ориентировочная<br>л. 87–89 — Ведомость объёмов работ |

| | | | | | | | | | |
|---|---|---|---|---|---|---|---|---|---|
| | | | | | | | ГД-2026-003-АИ | | |
| | | | | | | | Трёхкомнатная квартира<br>Общая площадь 78,95* м² · * размеры со скана, не замерены (реестр — п. 6–11, К-13) | | |
| Изм. | Кол.уч | Лист | № док. | Подп. | Дата | | Дизайн-проект интерьера трёхкомнатной квартиры | Стадия | Лист | Листов |
| Разраб. | | Кырпан А.С. | | | 05.10.26 | | | РП | 8 | 94 |
| Пров. | | | | | | | | | | |
| ГИП | | | | | | | | | | |
| | | | | | | | Открытые вопросы, принятые допущения и конфликты. Лист 3 из 6<br>М 6/м | Кырпан Александр Сергеевич | | |
| Н. контр. | | | | | | | | | | |
| Утв. | | | | | | | | | | |

# Открытые вопросы, принятые допущения и конфликты. Лист 4 из 6

ПРЕДВАРИТЕЛЬНО · не для производства работ · открыто пунктов: 31 (реестр — л. 6–11)

Сводка по реестрам координации

### Изменения проекта после выпуска листов (реестр изменений)

| № | Дата | Лист | Было | Стало | Кто решил, подпись |
|---|---|---|---|---|---|
| ИЗ-1 | 06.10.2026 | л. 39 — План выводов сантехники<br>л. 29 — План розеток и электровыводов<br>л. 41 — Спецификация сантехнического оборудования | В ванной и санузле 2 приборов отопления не было. | Добавлены электрические полотенцесушители IP44: П10 в ванной (480 мм, низ 900 мм) и П13 в санузле 2 (400 мм, низ 900 мм), выводы ЭФ6 и ЭВ7; мощность группы 13 — 2,4 кВт вместо 1,8 кВт. Основание: (в ванной и санузле есть полотенцесушитель — он же прибор отопления мокрой зоны); водяной не взят: стояка горячей воды в данных объекта нет, взят электрический IP44. Решение исполнителя: П10, П13, ЭФ6 и ЭВ7 остаются со знаком «**» (автором не подтверждены). | Утверждено: исполнитель по поручению Кырлана А.С., 05.10.2026. решение исполнителя |
| ИЗ-2 | 06.10.2026 | л. 50 — План полов<br>л. 51 — Ведомость отделки помещений | Ванная и санузел 2: пирог пола — стяжка 50 мм, слоя гидроизоляции в пироге не было. | Стяжка 33 мм и слой обмазочной гидроизоляции 2 мм (2 слоя, заведение на стены 200 мм); верх плиты — вровень с остальными помещениями. Основание: (в мокром помещении в пироге пола есть слой гидроизоляции с толщиной). Знак «**» у пола ванной и санузла 2 остаётся: решение исполнителя автором не подтверждено. | Утверждено: исполнитель по поручению Кырлана А.С., 05.10.2026. решение исполнителя |
| ИЗ-3 | 06.10.2026 | л. 31 — План выключателей и схема включения<br>л. 42 — Спецификация светильников и сценарии освещения | Кухня-гостиная: подвесы над столом (L14) и подсветка столешницы (L16) без светорегулятора, сценарии «Вечер» 50 % и «Ужин» 30 % недостижимы. | В выключателях S11 и S12 добавлены светорегуляторы (тип te); светильники Св42–Св44, лента подсветки и блок питания БП5 приняты диммируемыми. Основание: (промежуточный уровень сценария — только группе на светорегуляторе). Знак «**» у S11, S12, Св42–Св44 и БП5 остаётся. | Утверждено: исполнитель по поручению Кырлана А.С., 05.10.2026. решение исполнителя |
| ИЗ-4 | 06.10.2026 | л. 29 — План розеток и электровыводов<br>л. 82 — Развёртки стен А, Б. Санузел 2 (пом. 7) | Розетка Р33 (фен, санузел 2) на высоте 1200 мм, в перекрестье швов плитки. | Розетка Р33 на высоте 1100 мм, вне шва плитки. Затем высота снижена до 1000 мм вместе с Р7 и Р8 — запись ИЗ-9. Основание: (розетка — в центре плитки или на шве, не в перекрестье швов). | Утверждено: исполнитель по поручению Кырлана А.С., 05.10.2026. решение исполнителя |
| ИЗ-5 | 06.10.2026 | л. 59 — Встроенная мебель. Схема расположения<br>л. 63 — Кухня (пом. 6). Развёртка гарнитура | Кухня-гостиная: вывод «вытяжка» был, самой вытяжки в мебели не было; холодильник М6 описан только нишей. | Добавлена вытяжка над варочной панелью М15 (600 × 400 × 600 мм, низ 1600 мм); холодильник М6 описан как встраиваемый 60 см с вентзазорами в цоколе и под карнизом. Основание: (под вывод «вытяжка» и «холодильник» в помещении должна стоять сама техника). Знак «**» у М15 и М6 остаётся; проект кухни заказчиком не утверждён (К-6). | Утверждено: исполнитель по поручению Кырлана А.С., 05.10.2026. решение исполнителя |
| ИЗ-6 | 06.10.2026 | л. 26 — План расстановки мебели<br>л. 52 — Колерная карта | Марки: кухня К1…К14, шкафы П5 и П9, декор Д1…Д9. | Марки: мебель М (кухня М1…М14, шкафы М16 и М17), декор ДК1…ДК9; у полотенцесушителя санузла 2 — П13, потому что П11 занят мойкой. Позиции не менялись. В поле lightCheck образцов «D65 и лампа проекта» заменено на «D65, лампа проекта» (смысл прежний: два источника спичения). | Не утверждено: подписи нет. решение исполнителя |
| ИЗ-7 | 06.10.2026 | л. 62 — Шкаф-купе М16<br>л. 65 — Шкафы. Монтажная схема | Шкаф-купе (П5, ныне М16) 2600×600 мм: способ сборки не задан; диагональ боковины 2668 мм больше высоты до потолка 2620 мм. | Задана сборка стоя на месте (assembly: in-place): готовый корпус не поднять. Решение подтверждено автором 05.10.2026 (вопрос К-10 закрыт): размер корпуса не меняется, готовый корпус не поднять — сборка стоя на месте. | Утверждено: Кырлан А.С., автор проекта, 05.10.2026. решение автора проекта, оформлено исполнителем по его поручению (запись внесена разработчиком по замечанию проверки) |
| ИЗ-8 | 06.10.2026 | л. 29 — План розеток и электровыводов<br>л. 32, 33 — Ведомость электроточек и изделий | В ванной и санузле 2 не было вывода к вентилятору вытяжки и коробки уравнивания потенциалов. | Добавлены выводы к вентиляторам: ЭВ4 (ВР1, ванная) и ЭВ5 (ВР3, санузел 2) — группа 3, высота 2389 мм, включение с основным светом, таймер выбега в вентиляторе; и коробки уравнивания потенциалов КУП1 (ванная) и КУП2 (санузел 2) — высота 300 мм, у входа, вне зон 0–2, проводник от шины PE щита ЩК, сечение — по проекту ЭОМ. Основание: правила проверки (питание вентилятора вытяжки мокрого помещения) и (КУП в помещении с ванной или душем). Заказчик эти позиции не заказывал; решение исполнителя, ЭВ4, ЭВ5, КУП1 и КУП2 остаются со знаком «**» (автором поштучно не утверждены). | Утверждено: исполнитель по поручению Кырлана А.С., 05.10.2026. решение исполнителя |
| ИЗ-9 | 06.10.2026 | л. 29 — План розеток и электровыводов<br>л. 32, 33 — Ведомость электроточек и изделий | Розетки Р7 (стиральная машина) и Р8 (фен) в ванной — 1200 мм, Р33 (фен, санузел 2) — 1100 мм, с флагом решения: высота не обоснована назначением. | Р7, Р8 и Р33 на высоте 1000 мм — верхний предел нормы (ПУЭ, п. 6.6.30, не выше 1 м); флаг решения снят. Назначение стиральной машины и фена не требует большей высоты. Р12, Р17, Р18, Р19 и Р25 остались выше 1 м по назначению (решение исполнителя; основание записано в самой позиции, вопрос К-7): Р12, Р18 и Р19 — 1100 мм, в одной зоне с выводами ТВ и LAN, которые тоже на 1100 мм; Р17 — 1700 мм, рядом с ЩС на высоте щита (1700 мм); Р25 — 2000 мм, над нишей М6 за съёмной панелью с доступом, как и БП5. Высоты Р7, Р8, Р33 и всех перечисленных автором поштучно не подтверждены, знак «**» у них остаётся. | Утверждено: исполнитель по поручению Кырлана А.С., 05.10.2026. решение исполнителя |

| | | | | | | | |
|---|---|---|---|---|---|---|---|
| | | | | | | ГД-2026-003-АИ | |
| | | | | | | Трёхкомнатная квартира | |
| | | | | | | Общая площадь 78,95* м² · * размеры со скана, не замерены (реестр — п. 6–11, К-13) | |
| Изм. | Кол.уч | Лист | № док. | Подп. | Дата | Дизайн-проект интерьера трёхкомнатной квартиры | Стадия: РП; Лист: 9; Листов: 94 |
| Разраб. | | Кырлан А.С. | | | 05.10.26 | | |
| Пров. | | | | | | | |
| ГИП | | | | | | | |
| | | | | | | Открытые вопросы, принятые допущения и конфликты. Лист 4 из 6 | Кырлан Александр Сергеевич |
| Н. контр. | | | | | | М 6/м | |
| Утв. | | | | | | | |

выпуск 05.10.2026 № 6add39ab8d · стр. 11 из 137

# Открытые вопросы, принятые допущения и конфликты. Лист 5 из 6

Сводка по реестрам координации

### Изменения проекта после выпуска листов (реестр изменений) (продолжение)

| № | Дата | Лист | Было | Стало | Кто решил, подпись |
|---|---|---|---|---|---|
| ИЗ-10 | 06.10.2026 | л. 29 — План розеток и электровыводов<br>л. 32, 33 — Ведомость электроточек и изделий | Розетки Р7 (стиральная машина) и Р8 (фен) в ванной, Р33 (фен) в санузле 2 стояли в зоне 3 по ПУЭ, но ближе 2,5 м от границы зоны 1 по британской норме BS 7671 (п. 701.512.3); какая норма принята — вопрос К-6. | Принята норма ПУЭ (п. 7.1.48): розетки в зоне 3 помещения с ванной или душем допустимы при защите УЗО 30 мА. Положение розеток не менялось. Основание: розетки вне зон 0–2 (до границы зоны 1: Р7 — 650 мм, Р8 — 1220 мм, Р33 — 800 мм), исполнение IP44, группы 12 и 13 защищены УЗО 30 мА типа А. Это сознательное отступление от зарубежной нормы BS 7671: в России она не действует, по ней в таком месте допустима только бритвенная розетка с разделительным трансформатором. Высота розеток — отдельный вопрос К-7. | Утверждено: Кырпан А.С., автор проекта, 06.10.2026. решение автора проекта, оформлено исполнителем по его поручению |
| ИЗ-11 | 06.10.2026 | л. 39 — План выводов сантехники<br>л. 41 — Спецификация сантехнического оборудования<br>л. 29 — План розеток и электровыводов<br>л. 27, 28 — Спецификация мебели и оборудования | Ванная: стиральная машина П4 фронтальной загрузки 600 × 600 мм, габарит условный (модель не выбрана); перед люком ванна П1, свободно 50 мм вместо 500 — дверца не откроется (вопросы К-1, К-19). | Утверждена стиральная машина с вертикальной загрузкой, габарит в плане 400 × 600 мм (ширина 400 вдоль стены Б, глубина 600). На плане П4 уменьшена с 600 × 600 до 400 × 600, место у стены Б прежнее (500 мм от стены А), розетка Р7 остаётся на стене Б у машины. Габарит и тип загрузки — условие закупки, а не пожелание: машина с фронтальной загрузкой или большего габарита проекту не подходит (перед люком ванна П1). Условие записано в спецификации сантехнического оборудования, на листе выводов сантехники и в вопросе К-19 (задание на закупку). Модель по-прежнему не выбрана: габарит и подводку сверить по паспорту до закрытия трасс. Спецификация мебели и оборудования выводит габарит машины по осям плана — 600 × 400 мм: это тот же размер (глубина 600 в комнату, ширина 400 вдоль стены). | Утверждено: Кырпан А.С., автор проекта, 06.10.2026. решение автора проекта, оформлено исполнителем по его поручению |
| ИЗ-12 | 06.10.2026 | л. 63 — Кухня (пом. 6). Развёртка гарнитура<br>л. 29 — План розеток и электровыводов<br>л. 27, 28 — Спецификация мебели и оборудования | Кухня-гостиная: раскладка гарнитура и выводы техники приняты по типовой расстановке, проект кухни не утверждён (вопрос К-8). | Раскладка гарнитура принята проектной: мойка М7 у шахты Ш2, посудомоечная М14 рядом с мойкой, варочная панель и духовой шкаф в М8, вытяжка М15, холодильник М6. Условие: до начала черновых работ сверить раскладку и выводы техники с чертежом кухни от изготовителя; расхождения вносятся в реестр изменений, выводы пересматриваются по его чертежу. Проект кухни остаётся неутверждённым до этой сверки: позиции М7 и М8 сохраняют знак «*», примечание о выводах кухонной техники на листах сохранено, вопрос К-8 открыт. | Утверждено: Кырпан А.С., автор проекта, 06.10.2026. решение автора проекта, оформлено исполнителем по его поручению |
| ИЗ-13 | 06.10.2026 | л. 2 — Общие данные | Графы «Пров.» и «Н. контр.» основной надписи пусты (вопрос К-15); как с ними поступать — не записано. | Графы «Пров.» и «Н. контр.» остаются пустыми: независимой проверки и нормоконтроля проекта не было, автор проекта сам себе их не подписывает. Комплект выпускается предварительным: пока нет подписи проверяющего и нормоконтролёра, отличных от разработчика, он не считается окончательным. | Утверждено: Кырпан А.С., автор проекта, 06.10.2026. решение автора проекта, оформлено исполнителем по его поручению |
| ИЗ-14 | 06.10.2026 | л. 2 — Общие данные | Матрицы ответственности (делает / поставляет / принимает / хранит) нет; кто покупает и кто монтирует — не определено. | Принята типовая схема частного ремонта: материалы и оборудование покупает заказчик по спецификациям проекта; монтаж ведёт подрядная бригада; приёмку скрытых работ ведёт автор проекта; хранение — по договору подряда. Распределение закреплено по радиаторам, подоконникам, дверям и коробам скрытых дверей, розеткам и выключателям, сантехническим приборам, светильникам, отделочным материалам и плитке. Это схема по умолчанию, не факт: состав подрядчиков и поставщиков от заказчика не получен (вопрос К-22), схема уточняется договором подряда. | Не утверждено: подписи нет. решение исполнителя |
| ИЗ-15 | 06.10.2026 | л. 29 — План розеток и электровыводов<br>л. 32, 33 — Ведомость электроточек и изделий | Розетка Р7 (стиральная машина, ванная) на стене Б со смещением 685 мм: 348 мм от стояка холодной воды Ст В1-1 при практике приёмки не ближе 500 мм. | Р7 на стене Б со смещением 985 мм (на 300 мм дальше вдоль стены, по-прежнему у стиральной машины П4; высота 1000 мм прежняя): до стояка Ст В1-1 644 мм. Новое место — на шве плитки. Расстояние Р7 до границы зоны 1 стало 691 мм вместо 650 мм, названных в ИЗ-10; принятая там норма ПУЭ и положение Р8 и Р33 не затронуты. Положение стояков условно (К-17): отступ сделан от принятого положения, не от замера. Решение исполнителя; знак «*» у Р7 остаётся (высота вопрос К-7). | Не утверждено: подписи нет. решение исполнителя |
| ИЗ-16 | 06.10.2026 | л. 39 — План выводов сантехники<br>л. 40 — Схема разводки водопровода и канализации<br>л. 41 — Спецификация сантехнического оборудования<br>л. 86 — Узлы | Короб стояков Ш1 в углу ванной: в данных 180 × 450 мм (х 7890), на листе узлов 248 × 459 мм. Стояк канализации Ø110 с изоляцией 20 мм и просветом 40 мм до стенки в 180 мм не помещается: размер не годился ни как внутренний, ни как наружный. Стиральная машина П4 стояла в 50 мм от короба (у 500). | Один источник габарита: внутренний 195 × 406 мм (трубы Ст К1-1 Ø110 и Ст В1-1 Ø32, изоляция 20 мм, просвет 40 мм, считая от стен угла), обшивка 53 мм (профиль 28 + ГКЛВ 2 × 12,5) на свободных сторонах, наружный габарит каркаса 248 × 459 мм; короб остаётся в углу у стен (х 7822, у 0). Облицовка плиткой — сверх наружного габарита. Стиральная машина П4 сдвинута на 10 мм (у 510) — зазор до короба 51 мм при требовании не менее 50 мм. Положение стояков по-прежнему условно (К-17), размер короба пересчитывается по замеру. Решение исполнителя; знак «*» у стояков Ст К1-1 и Ст В1-1 (от них — положение и размер короба, К-17) и у машины П4 остаётся: автор их поштучно не утверждал. | Не утверждено: подписи нет. решение исполнителя |

| Изм. | Кол.уч | Лист | № док. | Подп. | Дата |
|---|---|---|---|---|---|
| Разраб. | | Кырпан А.С. | | | 05.10.26 |
| Пров. | | | | | |
| ГИП | | | | | |
| | | | | | |
| Н. контр. | | | | | |
| Утв. | | | | | |

**ГД-2026-003-АИ**

Трёхкомнатная квартира

Общая площадь 78,95* м² · * размеры со скана, не замерены (реестр — л. 6–11, К-13)

Дизайн-проект интерьера трёхкомнатной квартиры

| Стадия | Лист | Листов |
|---|---|---|
| РП | 10 | 94 |

**Открытые вопросы, принятые допущения и конфликты. Лист 5 из 6**

М 6/м

**Кырпан Александр Сергеевич**

выпуск 05.10.2026 № 6add39ab8d · стр. 12 из 137

# Открытые вопросы, принятые допущения и конфликты. Лист 6 из 6

Сводка по реестрам координации

### Изменения проекта после выпуска листов (реестр изменений) (продолжение)

| № | Дата | Лист | Было | Стало | Кто решил, подпись |
|---|---|---|---|---|---|
| ИЗ-17 | 06.10.2026 | л. 36 — План слаботочных сетей<br>л. 35 — План принципиальных трасс | Состав и места слаботочки в данных проекта заданы проектировщиком: щит слаботочный ЩС, точки доступа Wi-Fi AP1 и AP2. План заказчика их не содержит, подтверждения заказчика в данных нет. | Слаботочка остаётся предложением проектировщика, заказчиком не утверждена: щит слаботочный ЩС в Прихожей (стена Г, 3350 мм от угла, высота 1700 мм, рядом со щитом ЩК; ввод оптики, ONT, роутер, патч-панель), точка доступа AP1 в Прихожей (потолок, x 6800, y 6300) и точка доступа AP2 в Кухне-гостиной (потолок, x 12000, y 5500), питание PoE, кабель U/UTP кат. 6. Основание: (если заданы слаботочные точки, задан и слаботочный щит, к которому они сходятся); число и места точек доступа — ориентир практики «одна на 40–60 м²». Заказчик состав и места слаботочки не задавал и не подтверждал: решение исполнителя, знак «**» у ЩС, AP1 и AP2 остаётся до утверждения автором; число и места точек доступа проверить по замеру уровня сигнала после монтажа. | Не утверждено: подписи нет. решение исполнителя; предложение проектировщика, на утверждение А. С. Кырпана |

### Примечания

1. Номера листов — по ведомости рабочих чертежей комплекта (лист «Общие данные»).
2. Графа «Если решения нет» показывает состояние решения на листах; влияние на сроки и стоимость по пунктам не оценивалось.
3. Пункт, по которому принято решение, при следующем выпуске комплекта из таблиц исключается.

| Изм. | Кол.уч | Лист | № док. | Подп. | Дата | ГД-2026-003-АИ | | | |
|---|---|---|---|---|---|---|---|---|---|
| | | | | | | Трёхкомнатная квартира<br>Общая площадь 78,95* м² · * размеры со скана, не замерены (реестр — п. 6–11, К-13) | | | |
| Разраб. | | Кырпан А.С. | | | 05.10.26 | Дизайн-проект интерьера трёхкомнатной квартиры | Стадия | Лист | Листов |
| Пров. | | | | | | | РП | 11 | 94 |
| ГИП | | | | | | | | | |
| | | | | | | Открытые вопросы, принятые допущения и конфликты. Лист 6 из 6<br>М 6/м | Кырпан Александр Сергеевич | | |
| Н. контр. | | | | | | | | | |
| Утв. | | | | | | | | | |

выпуск 05.10.2026 · 6add39ab8d · стр. 13 из 137

# Задание на контрольный обмер и обследование. Лист 1 из 5

ПРЕДВАРИТЕЛЬНО · не для производства работ · открыто пунктов: 31 (реестр — л. 6–11)

Что замерить, вскрыть и получить до заказа материалов и изделий

Задание собрано из открытых вопросов, ответ на которые лежит на объекте или в документах, а не за столом проектировщика. Пока факт не получен, размер, материал или положение на листах — допущение (знак «*»), а не замер.
Сводка: на объекте — 17 (до демонтажа — 15; после демонтажа — 1; после черновых работ — 1); документом и при закупке — 9; из допущений в данных и на листах — 18, из них без вопроса в реестре — 4. Закрываются вопросы: К-2, К-8, К-11–К-14, К-17–К-21, К-23–К-28 (17). Вопросы, ждущие решения человека, задание не закрывает — они решаются по реестру открытых вопросов.

## Условия проведения

| Порядок работ | Приёмы и точность | Кто присутствует | Если факт не совпал с проектом |
|---|---|---|---|
| 1. До демонтажа — существующее состояние: контур, диагонали, высоты, проёмы, оси стояков, ниши и конструкции, которые видны.<br>2. После демонтажа, до черновых работ — то, что закрывали отделка и короба: основание стен, фактические толщины, углы, узлы.<br>3. После черновых работ, до чистового пола — габариты кухни и встроенной мебели по готовым стенам: после штукатурки и выравнивания размеры отличаются от размеров до работ.<br>4. Документы и данные закупки — не на объекте: к сроку из последней таблицы, от них зависят привязки и заказ.<br>Что заказывается по размеру из задания, до закрытия пункта не заказывают: сроки изготовления — по графику закупок прораба. | Обход по часовой стрелке от входа: стены, проёмы, потолок, коммуникации (стояки, щиток, вентканалы), особенности (ниши, короба, выступы).<br>Размеры записывают в мм; сумма участков равна общему размеру, при цепочке длиннее трёх участков ставят проверочный (общий) размер.<br>Диагонали каждого помещения; если две диагонали различаются на 5 мм и больше, разницу подписывают на плане.<br>Потолок — в нескольких точках: центр, углы, у проёмов. Проём — ширина, высота, глубина откоса, привязка к ближайшим углам, высота подоконника.<br>Допустимая погрешность прибора — 2–3 мм на метр; размеры округляют кратно 5 мм; два контрольных промера одного размера не должны расходиться более чем на 2 %. Допуск по пункту — в графе «Точность».<br>План БТИ обмер не заменяет. | Прораб (отвечает за проведение) — назначает день и порядок обхода, открывает объект и освобождает помещения, ведёт это задание и реестр изменений.<br>Архитектор — выполняет обмер, составляет акт контрольного обмера и подписывает результаты по размерам и конструкциям.<br>Владельцы вопросов присутствуют при пунктах своего раздела или принимают результат до заказа: Плиточник — К-2; Мебельщик — К-8, К-24; Инженер-электрик — К-14; позиции О-1; Инженер ВК (вода, канализация) К-17, К-19; Отделочник — К-23; позиции О-16; Прораб-координатор — К-28; Инженер ОВ — позиции О-2, О-3.<br>Технадзор — при вскрытиях и обследованиях: фото с рулеткой до закрытия.<br>Заказчик или его представитель — передаёт документы (план БТИ, проект дома, технические условия, паспорта), подписывает акт. Проектных решений на обмере не принимают: обмер даёт факт, решения — по реестру открытых вопросов (листы 6–11). | 1. В пределах допуска пункта — принимается измеренное значение, лист перевыпускается, знак «*» снимается.<br>2. Больше допуска или контрольные промеры расходятся более чем на 2 % — промер повторяют; не подтвердилось — запись в реестр изменений (дата, лист, было, стало, кто решил, подпись), работы в этом месте не начинают.<br>3. Затронуты несущая стена, стояк, вентканал или мокрая зона — сразу владельцу раздела и ГИПу (главному инженеру проекта); между разделами не больше двух кругов, затем решает ГИП.<br>4. На объекте устно ничего не согласуется: каждое решение — записью в реестр с подписью. |

## Этап 1. До демонтажа

| № | Где | Способ | Что сделать | Кто выполняет | Точность | Что пересчитается в альбоме | Чем подтверждается | Закрывает вопросы реестра |
|---|---|---|---|---|---|---|---|---|
| О-1 | Вход в квартиру или лестничная клетка; место щита на плане | Обмер | Существующий щиток и счётчик электроэнергии: место и габарит ниши, состояние ввода, марка и сечение вводного кабеля, наличие вводного автомата и УЗО, пломбы. | Архитектор | ±5 мм | Ниша и место щита на листах; вводной кабель и аппараты на однолинейной схеме; расстояния до первых групп.<br>Листы:<br>п. 34 — Однолинейная схема щита | акт контрольного обмера; фото с рулеткой и привязкой к стене или углу | Вопроса в реестре нет: Альбом принимает щит и ввод без осмотра.<br>Результат принимает:<br>Инженер-электрик |
| О-2 | Спальня 1 (пом. 1), Спальня 2 (пом. 4), Кухня-гостиная (пом. 6); у окон | Обмер | Положение стояков отопления (подающий и обратный) от граней стен, диаметры, наличие запорной арматуры; существующие радиаторы: число секций, межосевое расстояние, подводки. В данных стояков отопления нет — лист отопления выводит их условно у откоса окна, радиаторы — «принципиально, по расчёту». | Архитектор | ±5 мм | План отопления: места стояков и подводок, привязки радиаторов; подбор радиаторов по теплотехническому расчёту; радиаторы и узлы подключения в ВОР и спецификации.<br>Листы:<br>п. 36 — План отопления | акт контрольного обмера; фото с рулеткой и привязкой к стене или углу | Вопроса в реестре нет: Альбом принимает положение стояков и радиаторов отопления без обмера.<br>Результат принимает: Инженер ОВ |
| О-3 | Ванная (пом. 2), Кухня-гостиная (пом. 6), Санузел 2 (пом. 7) | Обмер | Положение и сечение вентканалов кухни и санузлов, проверка тяги (по листку бумаги или анемометром), состояние решёток. В данных каналов нет: лист вентиляции ставит решётки и вход вытяжки у стояков по практике. | Архитектор | ±5 мм | План вентиляции: места решёток и вход вытяжки; воздухообмен по помещениям; каналы не сужать и не закрывать (Постановление Госстроя № 170, п. 1.7.2).<br>Листы:<br>п. 37 — План вентиляции | акт контрольного обмера; фото с рулеткой и привязкой к стене или углу | Вопроса в реестре нет: Альбом ставит вентиляционные выводы без обмера каналов.<br>Результат принимает: Инженер ОВ |
| О-4 | Все помещения квартиры | Обмер | Высота потолка в каждом помещении в нескольких точках: центр, углы, у проёмов. Принято 2700 мм: на плане заказчика не указана. | Архитектор | ±5 мм | Вертикальные размеры альбома: развёртки, шкафы, плитка, объёмы работ; сборка шкафа-купе М16 (диагональ боковины 2868 мм против 2620 мм до потолка).<br>Листы:<br>п. 21 — Обмерный план | акт контрольного обмера | К-11<br>Результат принимает: Архитектор |

**Допущения и предложения на листе**

Основа листа: размеры сняты со скана плана заказчика по размерным цепочкам, контрольный обмер на объекте не выполнялся (К-13); высота потолка 2700 мм принята: на плане заказчика не указана (К-11); толщины стен приняты: наружные 250 мм, перегородки 150 мм (на плане 85–190 мм) (К-13); разрешённая мощность 15 кВт принята по типовой квартире, технических условий нет (К-14); утолщение стены 190 × 1360 мм и элемент 1470 × 160 мм плана заказчика не определены (К-12); ниши санузла 2 закрыты перегородкой и фальш-стеной: проектное решение, на плане заказчика ниша у входа открыта (К-18); несущие стены не определены: до технического заключения все существующие стены считаются несущими (К-20); окна существующие и сохраняются; подоконная доска и глубина откосов не заданы — приняты, не замерены (К-27).
См. лист открытых вопросов (лист 6, запись К-11; лист 7, записи К-12–К-14, К-18, К-20; лист 8, запись К-27).

| Изм. | Кол.уч | Лист | № док. | Подп. | Дата |
|---|---|---|---|---|---|
| Разраб. | | Кырпан А.С. | | | 05.10.26 |
| Пров. | | | | | |
| ГИП | | | | | |
| | | | | | |
| Н. контр. | | | | | |
| Утв. | | | | | |

**ГД-2026-003-АИ**

Трёхкомнатная квартира

Общая площадь 78,95* м² · * размеры со скана, не замерены (реестр — л. 6–11, К-13)

Дизайн-проект интерьера трёхкомнатной квартиры

| Стадия | Лист | Листов |
|---|---|---|
| РП | 12 | 94 |

**Задание на контрольный обмер и обследование.**
**Лист 1 из 5**
М 6/м

**Кырпан Александр Сергеевич**

выпуск 05.10.2026 № 6add39ab8d · стр. 14 из 137

# Задание на контрольный обмер и обследование. Лист 2 из 5

Что замерить, вскрыть и получить до заказа материалов и изделий

## Этап 1. До демонтажа (продолжение)

| № | Где | Способ | Что сделать | Кто выполняет | Точность | Что пересчитается в альбоме | Чем подтверждается | Закрывает вопросы реестра |
|---|---|---|---|---|---|---|---|---|
| О-5 | Гардеробная у спальни 2 (утолщение стены); кухня-гостиная, линия простенка (элемент 1470 × 160 мм) | Обследование | Определить назначение двух конструкций плана заказчика: утолщение стены 190 × 1360 мм (вентблок или пилон) и элемент 1470 × 160 мм (пилон, балка или барная стойка). | Архитектор | размеры ±5 мм | Показ элемента 1470 × 160 мм на листах (сейчас не показан, мебель от него свободна); обмерный план и план расстановки мебели.<br>Листы:<br>л. 21 — Обмерный план<br>л. 26 — План расстановки мебели | фото с рулеткой и привязкой к стене или углу; акт контрольного обмера | К-12<br>Результат принимает: Архитектор |
| О-6 | Вся квартира, все помещения; обход по часовой стрелке от входа | Обмер | Контрольный обмер всех помещений: чистые размеры по размерным цепочкам, толщины стен (приняты 250 мм наружные и 150 мм перегородки, на плане 85–190 мм), диагонали.<br>Отдельно проверить места, где принятое значение отличается от плана: ширина гардеробной 1070 мм (на плане 1120), ширина спальни 2 — 3130 мм (на плане 3120), привязка стены прихожей к спальне 1 (на плане стена 190 мм, в модели 150 мм). | Архитектор | ±5 мм; диагонали — разница от 5 мм подписывается | Чистые размеры и площади помещений, толщины стен; размеры, по которым заказываются материалы и изделия.<br>Листы:<br>л. 21 — Обмерный план | акт контрольного обмера | К-13, К-18<br>Результат принимает: Архитектор |
| О-7 | Все помещения; пол вскрыть до плиты в контрольных точках после снятия покрытий | Обмер | Нивелировка: отметка существующего пола и верха плиты перекрытия в каждом помещении и у порога входной двери — от одной сквозной отметки (нивелир или лазерный уровень). Верх плиты принят расчётом по пирогу пола (−0,064 от чистого пола), существующий пол в проекте не привязан. | Архитектор | ±5 мм; перепад плиты между помещениями размером на плане | Отметки ±0,000, −0,015 и −0,064; толщины стяжки по помещениям, объёмы стяжки и демонтажа пола.<br>Листы:<br>л. 21 — Обмерный план | акт контрольного обмера | К-13<br>Результат принимает: Архитектор |
| О-8 | Ванная (пом. 2), короб Ш1 248 × 459 мм: Ст К1-1*, Ст В1-1*; квартира, короб Ш2 270 × 1840 мм: Ст К1-2*, Ст В1-2*; наличие стояка ГВС, арматуры и счётчиков — по всей квартире | Обмер | Положение стояков Ст К1-1*, Ст В1-1*, Ст К1-2*, Ст В1-2*: привязка осей от граней стен, диаметры, размеры короба и люков. Стояк горячей воды Т3 в данных не задан, на листах ВК принят рядом с Ст В1-1*, Ст В1-2*: выяснить, есть ли он в доме, и где.<br>Отключающая арматура и счётчики воды на вводах: положение, тип, пломбы управляющей компании. Сверить до разметки выводов. | Архитектор | ±5 мм | Привязки выводов воды и канализации на планах выводов и разводки; расстояние розеток до стояка; места люков 300 × 400 мм; трассы Т3 и полотенцесушители (водяной или электрический); узлы ввода в спецификации ВК (краны, фильтры, счётчики).<br>Привязки выводов воды и канализации; расстояние розеток до стояка (К-1); места люков 300 × 400 мм.<br>Листы:<br>л. 39 — План выводов сантехники<br>л. 40 — Схема разводки водопровода и канализации | акт контрольного обмера; фото с рулеткой и привязкой к стене или углу | К-17<br>Результат принимает: Инженер ВК (вода, канализация) |
| О-9 | Все стены квартиры; специализированная организация либо конструктор по проекту дома | Обследование | Какие участки стен несущие: техническое заключение по результатам обследования. | Конструктор или специализированная организация | по заключению организации | Разметка несущих и ненесущих стен на обмерном плане и плане демонтажа; допустимость демонтажа, проёмов и штроб (пока все стены считаются несущими).<br>Листы:<br>л. 22 — План демонтажа и монтажа перегородок | техническое заключение; фото с рулеткой и привязкой к стене или углу | К-20<br>Результат принимает: Архитектор |
| О-10 | Спальня 1, ванная, гардеробная, прихожая, кухня-гостиная, санузел 2 | Обмер | Углы и диагонали помещений с кухней, санузлами, гардеробной и встроенной мебелью: длины сторон и обе диагонали каждого, отклонения углов от 90° у стен под встроенную мебель и плитку. Прямые углы отмечаются на листах только после этого замера. | Архитектор | ±5 мм; диагонали — разница от 5 мм подписывается | Отметки прямых углов 90°; размеры стен под встроенную мебель и плитку.<br>Листы:<br>л. 21 — Обмерный план<br>л. 26 — План расстановки мебели | акт контрольного обмера | К-21<br>Результат принимает: Архитектор |
| О-11 | Прихожая (пом. 5), стена В (входная дверь квартиры) | Обследование | Входная дверь Д-1: в какую сторону открывается полотно, где петли (левая или правая), что в проёме (коробка, наличники, откосы), ширина и высота проёма в чистоте. | Архитектор | ±5 мм | Дуга открывания и графа «Откр.» ведомости заполнения проёмов; позиция «Входная дверь» в ведомости объёмов работ и смете.<br>Листы:<br>л. 24 — План дверей и ведомость заполнения проёмов | фото с рулеткой и привязкой к стене или углу; акт контрольного обмера | К-26<br>Результат принимает: Архитектор |

**Допущения и предложения на листе**

Основа листа: размеры сняты со скана плана заказчика по размерным цепочкам, контрольный обмер на объекте не выполнялся (К-13); высота потолка 2700 мм принята: на плане заказчика не указана (К-11); толщины стен приняты: наружные 250 мм, перегородки 150 мм (на плане 85–190 мм) (К-13); разрешённая мощность 15 кВт принята по типовой квартире, технических условий нет (К-14); утолщение стены 190 × 1360 мм и элемент 1470 × 160 мм плана заказчика не определены (К-12); ниши санузла 2 закрыты перегородкой и фальш-стеной: проектное решение, на плане заказчика ниша у входа открыта (К-18); несущие стены не определены: до технического заключения все существующие стены считаются несущими (К-20); окна существующие и сохраняются; подоконная доска и глубина откосов не заданы — приняты, не замерены (К-27).

Знак «*» — принято, не замерено и не подтверждено [замерить на объекте]: К-17: Ст К1-1, Ст В1-1, Ст К1-2, Ст В1-2.

См. лист открытых вопросов (лист 6, запись К-11; лист 7, записи К-12–К-14, К-17, К-18, К-20; лист 8, запись К-27).

| Изм. | Кол.уч | Лист | № док. | Подп. | Дата |
|---|---|---|---|---|---|
| Разраб. | | Кырпан А.С. | | | 05.10.26 |
| Пров. | | | | | |
| ГИП | | | | | |
| | | | | | |
| Н. контр. | | | | | |
| Утв. | | | | | |

**ГД-2026-003-АИ**

Трёхкомнатная квартира

Общая площадь 78,95* м² · * размеры со скана, не замерены (реестр — л. 6–11, К-13)

| Дизайн-проект интерьера трёхкомнатной квартиры | Стадия | Лист | Листов |
|---|---|---|---|
| | РП | 13 | 94 |

**Задание на контрольный обмер и обследование.**
**Лист 2 из 5**
М 6/м

Кырпан Александр Сергеевич

выпуск 05.10.2026 № 6add39ab8d · стр. 15 из 137

# Задание на контрольный обмер и обследование. Лист 3 из 5

ПРЕДВАРИТЕЛЬНО · не для производства работ · открыто пунктов: 31 (реестр — л. 6–11)

Что замерить, вскрыть и получить до заказа материалов и изделий

### Этап 1. До демонтажа (продолжение)

| № | Где | Способ | Что сделать | Кто выполняет | Точность | Что пересчитается в альбоме | Чем подтверждается | Закрывает вопросы реестра |
|---|---|---|---|---|---|---|---|---|
| О-12 | Спальня 1 (пом. 1), спальня 2 (пом. 4), кухня-гостиная (пом. 6): все окна наружной стены | Обмер | Окна ОК-1…ОК-4: ширина и высота проёма, высота низа окна от пола, подоконная доска (есть или нет, вылет), глубина откоса и коробка окна, состояние блока. | Архитектор | ±5 мм | Откосы и подоконники в ведомости объёмов работ; размеры и высота низа окон в ведомости заполнения проёмов; шторы и карнизы у окон.<br>Листы:<br>п. 24 — План дверей и ведомость заполнения проёмов | акт контрольного обмера; фото с рулеткой и привязкой к стене или углу | К-27<br>Результат принимает: Архитектор |
| О-13 | По месту | Обмер | Подтвердить на объекте принятое: окна существующие и сохраняются; подоконная доска и глубина откосов не заданы приняты, не замерены | Архитектор | ±5 мм | Листы, где используется принятая величина.<br>Листы:<br>л. 2–5 — Общие данные | акт контрольного обмера | К-27<br>Результат принимает: Архитектор |
| О-14 | Прихожая (пом. 5): дверь пом. 5, стена В | Обмер | Дверь пом. 5, стена В: положение (привязки к ближайшим углам), ширина, высота, толщина стены в проёме. Принято в проекте: входная дверь существующая; по плану заказчика полотно открывается наружу, в общий коридор — направление взято с плана и на объекте не проверено; остаётся ли существующий блок или он заменяется — не решено (К-26). | Архитектор | ±5 мм | Проёмы на обмерном плане и в ведомости проёмов; привязки мебели и выводов к проёмам.<br>Листы:<br>п. 21 — Обмерный план<br>п. 24 — План дверей и ведомость заполнения проёмов | акт контрольного обмера; фото с рулеткой и привязкой к стене или углу | К-26<br>Результат принимает: Архитектор |
| О-15 | Спальня 1 (пом. 1), ванная (пом. 2), гардеробная (пом. 3), спальня 2 (пом. 4), коридор (пом. 8): дверные проёмы Д-2, Д-3, Д-4 | Обмер | Проёмы скрытых дверей Д-2 (спальня 1 и спальня 2), Д-3 и Д-4 в чистоте после снятия отделки: ширина и высота проёма, отвес и диагонали проёма, толщина стены в проёме (у Д-3 и Д-4 по скану 85 мм при принятых 150 мм), привязка проёма к углу помещения. Модель и размеры короба и полотна — по документам изготовителя выбранного блока. | Архитектор | ±5 мм; толщина стены ±5 мм | Размер проёма и привязки на плане дверей; размер полотна и короба в ведомости заполнения проёмов; узел скрытой двери (толщина стены 85 или 150 мм); заказ скрытых дверей.<br>Листы:<br>п. 24 — План дверей и ведомость заполнения проёмов<br>п. 86 — Узлы | акт контрольного обмера; фото с рулеткой и привязкой к стене или углу | К-25<br>Результат принимает: Архитектор |

### Этап 2. После демонтажа, до черновых работ

| № | Где | Способ | Что сделать | Кто выполняет | Точность | Что пересчитается в альбоме | Чем подтверждается | Закрывает вопросы реестра |
|---|---|---|---|---|---|---|---|---|
| О-16 | Спальня 1 (пом. 1), Ванная (пом. 2), Гардеробная (пом. 3), Спальня 2 (пом. 4), Прихожая (пом. 5), Кухня-гостиная (пом. 6), Санузел 2 (пом. 7), Коридор (пом. 8) | Обмер | Вертикаль и плоскостность стен: отклонение от вертикали по высоте стены (отвес или лазерный уровень), просвет под правилом 2 м, кривизна углов. Нужно там, где от стены зависит изделие: облицовка плиткой (пом. 2, 7), штукатурка и окраска (пом. 1, 2, 3, 4, 5, 6, 7, 8), встроенная мебель и кухня (пом. 1, 5, 6). | Архитектор | до 1 мм на 2 м (правило и клиновой щуп); вертикаль — мм на высоту стены, отклонения подписываются на плане | Толщина штукатурки и расход смеси в ВОР и спецификации; раскладка плитки (подрезка у стен); зазоры и крепление встроенной мебели и кухни.<br>Листы:<br>п. 46–49 — Раскладка плитки<br>п. 51 — Ведомость отделки помещений | акт контрольного обмера | Вопроса в реестре нет: Альбом принимает стены ровными и вертикальными без замера.<br>Результат принимает: Отделочник |

**Допущения и предложения на листе**

Основа листа: размеры сняты со скана плана заказчика по размерным цепочкам, контрольный обмер на объекте не выполнялся (К-13); высота потолка 2700 мм принята: на плане заказчика не указана (К-11); толщины стен приняты: наружные 250 мм, перегородки 150 мм (на плане 85–190 мм) (К-13); разрешённая мощность 15 кВт принята по типовой квартире, технических условий нет (К-14); утолщение стены 190 × 1360 мм и элемент 1470 × 160 мм плана заказчика не определены (К-12); ниши санузла 2 закрыты перегородкой и фальш-стеной: проектное решение, на плане заказчика ниша у входа открыта (К-18); несущие стены не определены: до технического заключения все существующие стены считаются несущими (К-20); окна существующие и сохраняются; подоконная доска и глубина откосов не заданы — приняты, не замерены (К-27).

См. лист открытых вопросов (лист 6, запись К-11; лист 7, записи К-12–К-14, К-18, К-20; лист 8, запись К-27).

| Изм. | Кол.уч | Лист | № док. | Подп. | Дата |
|---|---|---|---|---|---|
| Разраб. | | Кырпан А.С. | | | 05.10.26 |
| Пров. | | | | | |
| ГИП | | | | | |
| | | | | | |
| Н. контр. | | | | | |
| Утв. | | | | | |

**ГД-2026-003-АИ**

Трёхкомнатная квартира

Общая площадь 78,95* м² · * размеры со скана, не замерены (реестр — п. 6–11, К-13)

Дизайн-проект интерьера трёхкомнатной квартиры

| Стадия | Лист | Листов |
|---|---|---|
| РП | 14 | 94 |

**Задание на контрольный обмер и обследование.**
**Лист 3 из 5**
М 6/м

Кырпан Александр Сергеевич

выпуск 05.10.2026 · 6add39ab8d · стр. 16 из 137

# Задание на контрольный обмер и обследование. Лист 4 из 5

Что замерить, вскрыть и получить до заказа материалов и изделий

### Этап 3. После черновых работ, до чистового пола

| № | Где | Способ | Что сделать | Кто выполняет | Точность | Что пересчитается в альбоме | Чем подтверждается | Закрывает вопросы реестра |
|---|---|---|---|---|---|---|---|---|
| О-17 | Кухня-гостиная (пом. 6), зона кухни | Обмер | Габариты кухни по готовым стенам: размеры после штукатурки и выравнивания, отметки чистых стен под гарнитур. | Архитектор | ±5 мм | Размеры гарнитура и привязки выводов техники к чистым стенам.<br>Листы:<br>л. 63 — Кухня (пом. 6). Развёртка гарнитура<br>л. 29 — План розеток и электровыводов | акт контрольного обмера | К-8<br>Результат принимает: Мебельщик |

### Документы и данные закупки (не на объекте)

| № | У кого, откуда | Способ | Что получить | К какому сроку | Что пересчитается в альбоме | Чем подтверждается | Закрывает вопросы реестра |
|---|---|---|---|---|---|---|---|
| О-18 | Образец и паспорт партии от поставщика плитки | Закупка | Артикул плитки и калибр партии (фактический размер плитки) для ванной и санузла 2. | До заказа плитки и раскладки | Раскладка плиток: пол 600 × 600 мм и стены 600 × 1200 мм приняты по номинальным размерам; подрезка у стен; количество плитки.<br>Листы:<br>л. 46 — Раскладка плитки. Планы полов<br>л. 48 — Раскладка плитки. Ванная. Развёртки стен<br>л. 49 — Раскладка плитки. Санузел 2. Развёртки стен | паспорт изделия или партии; образец | К-2<br>Результат принимает: Плиточник |
| О-19 | Заказчик; организация, выдавшая технические условия | Документ | Технические условия на присоединение: разрешённая мощность (принято 15 кВт по типовой квартире, расчётная 11,8 кВт). | До утверждения однолинейной схемы щита | Однолинейная схема щита: вводной аппарат и группы; сверка расчётной мощности 11,8 кВт с разрешённой.<br>Листы:<br>л. 34 — Однолинейная схема щита | копия документа | К-14<br>Результат принимает: Инженер-электрик |
| О-20 | Заказчик (документы на квартиру и дом) | Документ | Проект дома и план БТИ: тип и серия дома, какие стены несущие. | До любого демонтажа, проёмов и штробления в стенах | Разметка несущих и ненесущих стен на обмерном плане и плане демонтажа; допустимость демонтажа, проёмов и штроб (пока все стены считаются несущими).<br>Листы:<br>л. 22 — План демонтажа и монтажа перегородок | копия документа | К-20<br>Результат принимает: Архитектор |
| О-21 | Образцы и паспорта изделий от поставщика; код изделия производителя | Закупка | Артикулы изделий отделки: инженерная доска 14/4 мм (дуб натуральный, масло, 1-полосная); керамогранит пола ректифицированный под травертин, матовый, 600 × 600 × 9 мм (пом. 2, 7) и 600 × 1200 × 9 мм (пом. 5); керамогранит стен под травертин, матовый, 600 × 1200 × 9 мм (пом. 2, 7); керамогранит фартука кухни 1200 × 600 × 9 мм (пом. 6); плинтус МДФ под покраску 80 × 16 мм. | До заказа материалов | Ведомость отделки помещений, спецификации материалов, количество упаковок и смета: подсчёт по номинальным размерам заменить подсчётом по выбранным изделиям.<br>Листы:<br>л. 46 — Раскладка плитки. Планы полов<br>л. 47 — Раскладка плитки. Прихожая. Фартук кухни<br>л. 48 — Раскладка плитки. Ванная. Развёртки стен<br>л. 49 — Раскладка плитки. Санузел 2. Развёртки стен<br>л. 50 — План полов<br>л. 51 — Ведомость отделки помещений<br>л. 53 — Спецификация отделочных материалов<br>л. 67 — Реестр марок отделки и позиций альбома<br>л. 90–92 — Спецификация материалов<br>л. 93, 94 — Смета ориентировочная | паспорт изделия или партии; образец | К-23<br>Результат принимает: Отделочник |
| О-22 | Поставщик или изготовитель техники; паспорт и монтажная схема выбранной модели | Закупка | Модели и монтажные схемы встраиваемой техники: холодильник (М6**) и посудомоечная машина (М14*) — габариты ниши, вентзазоры, высота цоколя и решётки, подключение; модель вытяжки М15** и её паспорт. | До заказа модулей кухни | Размеры ниш модулей М6** и М14*; вентиляция в цоколе и за корпусом; точки подключения техники на листе кухни.<br>Листы:<br>л. 63 — Кухня (пом. 6). Развёртка гарнитура<br>л. 64 — Кухня (пом. 6). Монтажная схема | паспорт изделия или партии | К-24<br>Результат принимает: Мебельщик |

**Допущения и предложения на листе**

Основа листа: размеры сняты со скана плана заказчика по размерным цепочкам, контрольный обмер на объекте не выполнялся (К-13); высота потолка 2700 мм принята: на плане заказчика не указана (К-11); толщины стен приняты: наружные 250 мм, перегородки 150 мм (на плане 85–190 мм) (К-13); разрешённая мощность 15 кВт принята по типовой квартире, технических условий нет (К-14); утолщение стены 190 × 1360 мм и элемент 1470 × 160 мм плана заказчика не определены (К-12); ниши санузла 2 закрыты перегородкой и фальш-стеной: проектное решение, на плане заказчика ниша у входа открыта (К-18); несущие стены не определены: до технического заключения все существующие стены считаются несущими (К-20); окна существующие и сохраняются; подоконная доска и глубина откосов не заданы — приняты, не замерены (К-27).

Знак «*» — принято, не замерено и не подтверждено (замерить на объекте): К-8: М14.

Знак «**» — предложение проектировщика, заказчиком не утверждено (согласовать с заказчиком): ИЗ-5, К-8: М6, М15.

См. лист открытых вопросов (лист 6, записи К-8, К-11; лист 7, записи К-12–К-14, К-18, К-20; лист 8, запись К-27; лист 9, запись ИЗ-5).

| Изм. | Кол.уч | Лист | № док. | Подп. | Дата |
|---|---|---|---|---|---|
| Разраб. | | Кырпан А.С. | | | 05.10.26 |
| Пров. | | | | | |
| ГИП | | | | | |
| | | | | | |
| Н. контр. | | | | | |
| Утв. | | | | | |

**ГД-2026-003-АИ**

Трёхкомнатная квартира

Общая площадь 78,95* м² · * размеры со скана, не замерены (реестр — л. 6–11, К-13)

| Дизайн-проект интерьера трёхкомнатной квартиры | Стадия | Лист | Листов |
|---|---|---|---|
| | РП | 15 | 94 |
| **Задание на контрольный обмер и обследование. Лист 4 из 5**<br>М 6/м | **Кырпан Александр Сергеевич** | | |

выпуск 05.10.2026 · 6add39ab8d · стр. 17 из 137

# Задание на контрольный обмер и обследование. Лист 5 из 5

Что замерить, вскрыть и получить до заказа материалов и изделий

## Документы и данные закупки (не на объекте) (продолжение)

| № | У кого, откуда | Способ | Что получить | К какому сроку | Что пересчитается в альбоме | Чем подтверждается | Закрывает вопросы реестра |
|---|---|---|---|---|---|---|---|
| О-23 | Поставщики и изготовители выбранных изделий | Закупка | Срок поставки или изготовления каждой позиции с длинной поставкой: скрытые двери (короб и полотно), кухонный гарнитур, встраиваемая техника, керамогранит, инженерная доска, сантехника и инсталляции, встроенная мебель по замеру цеха после выбора модели, в письменном виде. | До назначения даты заказа каждой позиции | График закупок и работ: срок поставки и последний срок заказа по каждой позиции; смета ориентировочная: графа «Срок поставки»; ведомость объёмов работ.<br>Листы:<br>л. 17–20 — График закупок и работ<br>л. 93, 94 — Смета ориентировочная<br>л. 87–89 — Ведомость объёмов работ | копия документа | К-28<br>Результат принимает: Прораб-координатор |
| О-24 | Поставщик стиральной машины; модель пока не выбрана | Закупка | Паспорт или монтажная схема выбранной модели: П4* — габарит, высота, тип загрузки, положение подводки и слива. Принято в проекте: вертикальная загрузка 400 × 600 мм — условие закупки (решение автора, ИЗ-11); модель не выбрана, габарит сверить по паспорту. | До закрытия люка и разводки | Габариты и положение изделий на планах и развёртках, выводы (вода, слив, электро), монтажные зазоры; знак «*» у марки снимается паспортом или чертежом.<br>Габарит и подводка П4*; зазоры в ванной (К-1).<br>Листы:<br>л. 39 — План выводов сантехники<br>л. 41 — Спецификация сантехнического оборудования | паспорт изделия или партии | К-19<br>Результат принимает: Инженер ВК (вода, канализация) |
| О-25 | Изготовитель кухонного гарнитура; проект кухни заказчиком не утверждён | Документ | Чертёж или монтажная схема изготовителя: М7* (модуль нижний с мойкой) — габарит мойки, положение смесителя и сифона, высота рабочей поверхности, М14* (модуль под встраиваемую посудомоечную машину) — габарит ниши, положение подводки и слива, мощность, М8* (модуль нижний) — габариты, положение и выводы (вода, слив, электро) по паспорту выбранной модели. Принято в проекте: М7*: габарит 800 × 600 мм — по данным проекта, не по паспорту, М14*: габарит 600 × 600 мм — по данным проекта, не по паспорту, М8*: габарит 1800 × 600 мм — по данным проекта, не по паспорту. | До черновой электрики и сантехники кухни | Габариты и положение изделий на планах и развёртках, выводы (вода, слив, электро), монтажные зазоры; знак «*» у марки снимается паспортом или чертежом.<br>Выводы кухонной техники на планах розеток и выводов; развёртка гарнитура.<br>Листы:<br>л. 63 — Кухня (пом. 6). Развёртка гарнитура<br>л. 29 — План розеток и электровыводов | копия документа | К-8<br>Результат принимает: Мебельщик |
| О-26 | Поставщик изделий: Кухня-гостиная (пом. 6) | Закупка | Паспорт или монтажная схема выбранной модели: П11* (мойка кухонная врезная) — габарит мойки, положение смесителя и сифона, высота рабочей поверхности, П12* (посудомоечная машина встраиваемая) — габарит ниши, положение подводки и слива, мощность. Принято в проекте: П11*: габарит 500 × 450 мм — по данным проекта, не по паспорту, П12*: габарит 600 × 600 мм — по данным проекта, не по паспорту. | До закрытия трасс и разводки | Габариты и положение изделий на планах и развёртках, выводы (вода, слив, электро), монтажные зазоры; знак «*» у марки снимается паспортом или чертежом.<br>Листы:<br>л. 26 — План расстановки мебели | паспорт изделия или партии | К-8<br>Результат принимает: Мебельщик |

## Примечания

1. Подтверждение: акт контрольного обмера (дата, кто присутствовал, прибор, перечень промеров с результатами, подписи присутствующих); к акту — фото вскрытий и узлов и техническое заключение организации, выполнившей обследование.
2. Номера листов — по ведомости рабочих чертежей комплекта (лист «Общие данные»).
3. Пункт исключается из задания при следующем выпуске, когда акт подписан, значение внесено в проект и листы перевыпущены; знак «*» у величины снимается только замером.

**Допущения и предложения на листе**

Основа листа: размеры сняты со скана плана заказчика по размерным цепочкам, контрольный обмер на объекте не выполнялся (К-13); высота потолка 2700 мм принята: на плане заказчика не указана (К-11); толщины стен приняты: наружные 250 мм, перегородки 150 мм (на плане 85–190 мм) (К-13); разрешённая мощность 15 кВт принята по типовой квартире, технических условий нет (К-14); утолщение стены 190 × 1360 мм и элемент 1470 × 160 мм плана заказчика не определены (К-12); ниши санузла 2 закрыты перегородкой и фальш-стеной: проектное решение, на плане заказчика ниша у входа открыта (К-18); несущие стены не определены: до технического заключения все существующие стены считаются несущими (К-20); окна существующие и сохраняются; подоконная доска и глубина откосов не заданы — приняты, не замерены (К-27).

Знак «*» — принято, не замерено и не подтверждено (замерить на объекте): ИЗ-11, К-19: П4 — вертикальная загрузка 400 × 600 мм — условие закупки (решение автора, ИЗ-11); модель не выбрана, габарит сверить по паспорту; К-8: М7, М14, М8, П11, П12.

См. лист открытых вопросов (лист 6, записи К-8, К-11; лист 7, записи К-12–К-14, К-18–К-20; лист 8, запись К-27; лист 10, запись ИЗ-11).

| Изм. | Кол.уч | Лист | № док. | Подп. | Дата | ГД-2026-003-АИ | | | |
|---|---|---|---|---|---|---|---|---|---|
| | | | | | | Трёхкомнатная квартира<br>Общая площадь 78,95* м² · * размеры со скана, не замерены (реестр — л. 6–11, К-13) | | | |
| Разраб. | | Кырлан А.С. | | | 05.10.26 | Дизайн-проект интерьера трёхкомнатной квартиры | Стадия | Лист | Листов |
| Пров. | | | | | | | РП | 16 | 94 |
| ГИП | | | | | | | | | |
| Н. контр. | | | | | | Задание на контрольный обмер и обследование. Лист 5 из 5<br>М 6/м | Кырлан Александр Сергеевич | | |
| Утв. | | | | | | | | | |

выпуск 05.10.2026 · 6add39ab8d · стр. 18 из 137

ПРЕДВАРИТЕЛЬНО · не для производства работ · открыто пунктов: 31 (реестр — л. 6–11)

# График закупок и работ. Лист 1 из 4

Что заказывать и когда не раньше чего: относительный порядок без дат; срок поставки — из данных или «уточняется у поставщика»

Лист не содержит дат: контрольного обмера, подписанных решений автора и договоров ещё нет, и любая дата была бы выдумана. Вместо календаря — порядок и условия: замер → решение и выбор изделия → заказ → срок поставки → работа, которую позиция блокирует.
Срок поставки печатается как срок, только если он задан в данных позиции. Нет — «срок уточняется у поставщика» и ссылка на вопрос реестра о сроках; типовой диапазон практики стоит рядом как ориентир и заказывать по нему нельзя. Номера З-N и Р-N — строки этого листа, К-N — записи реестра открытых вопросов, О-N — позиции задания на контрольный обмер.

## Закупки: что заказывается, от чего зависит заказ и какую работу блокирует

| № | Позиция и где | 1. Замер до заказа | 2. Решение, выбор изделия, паспорт | 3. Условие заказа | 4. Срок поставки | 5. Блокирует работу | Закрывает вопросы реестра |
|---|---|---|---|---|---|---|---|
| З-1 | Двери скрытого монтажа с коробом под покраску в новой перегородке П-1**: Д-5 — 1 шт.<br>пом. 6 | О-15: обмер: Спальня 1 (пом. 1), ванная (пом. 2), гардеробная (пом. 3), спальня 2 (пом. 4), коридор (пом. 8): дверные проёмы Д-2, Д-3, Д-4 (К-25)<br>О-6: обмер: Вся квартира, все помещения; обход по часовой стрелке от входа (К-13, К-18) | Скрытые двери Д-2 (спальня 1 и спальня 2), Д-3 (ванная) и Д-4 (гардеробная) заданы размером проёма 800×2100 со скана плана заказчика; проёмы существующие, расширять их до технического заключения (К-20) нельзя. (К-25)<br>Санузел 2: ниша 1600 × 1840 мм у входа закрыта перегородкой, ниша 660 × 260 мм (уступ по плану) — фальш-стеной с рамой инсталляции: проектное решение, на плане заказчика ниша у входа открыта в кухню-гостиную. (К-18)<br>Вход в санузел 2 (с унитазом) — из кухни-гостиной: так по плану заказчика (ниша у входа на плане открыта в кухню-гостиную, в проекте закрыта перегородкой по линии низа прихожей). (К-4) | После 1 и 2 и после получения срока у поставщика (К-28); дата заказа — когда срок известен, не позднее чем за срок до начала Р-3. | срок уточняется у поставщика<br>Ориентир практики (не срок поставщика): ≈ 30 дн. | Р-3 «перегородки ГКЛ»: коробку ставят в каркас перегородки до обшивки (работа по перегородкам); полотно навешивают после чистовой отделки стен | К-4, К-13, К-18, К-25, К-28 |
| З-2 | Двери скрытого монтажа с коробом под покраску в существующих проёмах: Д-2, Д-3, Д-4 — 4 шт.<br>пом. 1, 4, 8 | О-15: обмер: Спальня 1 (пом. 1), ванная (пом. 2), гардеробная (пом. 3), спальня 2 (пом. 4), коридор (пом. 8): дверные проёмы Д-2, Д-3, Д-4 (К-25)<br>О-6: обмер: Вся квартира, все помещения; обход по часовой стрелке от входа (К-13, К-18) | Скрытые двери Д-2 (спальня 1 и спальня 2), Д-3 (ванная) и Д-4 (гардеробная) заданы размером проёма 800×2100 со скана плана заказчика; проёмы существующие, расширять их до технического заключения (К-20) нельзя. (К-25) | После 1 и 2 и после получения срока у поставщика (К-28); дата заказа — когда срок известен, не позднее чем за срок до начала Р-6. | срок уточняется у поставщика<br>Ориентир практики (не срок поставщика): ≈ 30 дн. | Р-6 «штукатурка»: короб ставят до штукатурки (коробку ставят на черновой стадии; полотно навешивают после чистовой отделки стен) | К-13, К-18, К-25, К-28 |
| З-3 | Кухонный гарнитур по проекту кухни: модули М6**, М7*, М14*, М8*, М13, М15**<br>пом. 6 | О-17: обмер: Кухня-гостиная (пом. 6), зона кухни (К-8) | О-25: Чертёж или монтажная схема изготовителя: М7* (модуль нижний с мойкой) — габарит мойки, положение смесителя и сифона, высота рабочей поверхности, М14* (модуль под встраиваемую посудомоечную машину) габарит ниши, положение подводки и слива, мощность, М8* (модуль нижний) габариты, положение и выводы (вода, слив, электро) по паспорту выбранной модели. (К-8); до черновой электрики и сантехники кухни<br>Проект кухни не утверждён заказчиком: выводы кухонной техники (мойка М7*, посудомоечная М14*, варочная панель и духовой шкаф М8*, вытяжка М15**, холодильник М6**) приняты по типовой расстановке техники. (К-8) | После 1 и 2 и после получения срока у поставщика (К-28); дата заказа — когда срок известен, не позднее чем за срок до начала Р-16. | срок уточняется у поставщика<br>Ориентир практики (не срок поставщика): 4–8 нед. от замера | Р-16 «кухня и мебель»: замер кухни — по готовым стенам после штукатурки или плитки, до чистового пола; производство идёт параллельно со стяжкой и отделкой | К-8, К-28 |

**Допущения и предложения на листе**

Основа листа: размеры сняты со скана плана заказчика по размерным цепочкам, контрольный обмер на объекте не выполнялся (К-13); высота потолка 2700 мм принята: на плане заказчика не указана (К-11); толщины стен приняты: наружные 250 мм, перегородки 150 мм (на плане 85–190 мм) (К-13); разрешённая мощность 15 кВт принята по типовой квартире, технических условий нет (К-14); утолщение стены 190 × 1360 мм и элемент 1470 × 160 мм плана заказчика не определены (К-12); ниши санузла 2 закрыты перегородкой и фальш-стеной: проектное решение, на плане заказчика ниша у входа открыта (К-18); несущие стены не определены: до технического заключения все существующие стены считаются несущими (К-20); окна существующие и сохраняются; подоконная доска и глубина откосов не заданы — приняты, не замерены (К-27).

Знак «*» — принято, не замерено и не подтверждено (замерить на объекте): К-8: М7, М14, М8.

Знак «**» — предложение проектировщика, заказчиком не утверждено (согласовать с заказчиком): ИЗ-5, К-8: М6, М15; К-4, К-18: П-1 — проектное решение исполнителя: на плане заказчика ниша у входа открыта в кухню-гостиную; конструкция не утверждена автором (вопрос К-18), положение и размеры сняты со скана (К-13).

Открытые вопросы и конфликты по листу: К-28.

См. лист открытых вопросов (лист 6, записи К-4, К-8, К-11; лист 7, записи К-12–К-14, К-18, К-20; лист 8, записи К-27, К-28; лист 9, запись ИЗ-5).

| | | | | | | | |
|---|---|---|---|---|---|---|---|
| | | | | | | ГД-2026-003-АИ | |
| | | | | | | Трёхкомнатная квартира | |
| | | | | | | Общая площадь 78,95* м² · * размеры со скана, не замерены (реестр — п. 6–11, К-13) | |
| Изм. | Кол.уч | Лист | № док. | Подп. | Дата | Дизайн-проект интерьера трёхкомнатной квартиры | Стадия: РП; Лист: 17; Листов: 94 |
| Разраб. | | Кырпан А.С. | | | 05.10.26 | | |
| Пров. | | | | | | | |
| ГИП | | | | | | | |
| | | | | | | | |
| Н. контр. | | | | | | График закупок и работ. Лист 1 из 4 | Кырпан Александр Сергеевич |
| Утв. | | | | | | М 6/м | |

выпуск 05.10.2026 № 6add39ab8d · стр. 19 из 137

# График закупок и работ. Лист 2 из 4

Что заказывать и когда не раньше чего: относительный порядок без дат; срок поставки — из данных или «уточняется у поставщика»

## Закупки: что заказывается, от чего зависит заказ и какую работу блокирует (продолжение)

| № | Позиция и где | 1. Замер до заказа | 2. Решение, выбор изделия, паспорт | 3. Условие заказа | 4. Срок поставки | 5. Блокирует работу | Закрывает вопросы реестра |
|---|---|---|---|---|---|---|---|
| З-4 | Встраиваемая техника кухни: М6** холодильник, М14* посудомоечная машина, М15** вытяжка<br>пом. 6 | | О-22: Модели и монтажные схемы встраиваемой техники: холодильник (М6**) и посудомоечная машина (М14*) — габариты ниши, вентзазоры, высота цоколя и решётки, подключение; модель вытяжки М15** и её паспорт. (К-24); до заказа модулей кухни | После 1 и 2 и после получения срока у поставщика (К-28); дата заказа — когда срок известен, не позднее чем за срок до начала Р-16. | срок уточняется у поставщика | Р-16 «кухня и мебель»: паспорта и монтажные схемы — до изготовления модулей кухни: нишу и вентзазоры задаёт модель, а не типовая схема 60 см | К-24, К-28 |
| З-5 | Стиральная машина: П4* (вертикальная загрузка 400 × 600 мм — условие закупки)<br>пом. 2 | | О-24: Паспорт или монтажная схема выбранной модели: П4* — габарит, высота, тип загрузки, положение подводки и слива. (К-19); до закрытия люка и разводки | После 1 и 2 и после получения срока у поставщика (К-28); дата заказа — когда срок известен, не позднее чем за срок до начала Р-5. | срок уточняется у поставщика | Р-5 «черновая сантехника»: габарит и подводка — до закрытия люка и разводки | К-19, К-28 |
| З-6 | Сантехнические приборы и инсталляции: П1, П2, П3, П11*, П6, П7, П8<br>пом. 2, 6, 7 | О-8: обмер: Ванная (пом. 2), короб Ш1 248 × 459 мм: Ст К1-1*, Ст В1-1*; квартира, короб Ш2 270 × 1840 мм: Ст К1-2*, Ст В1-2*; наличие стояка ГВС, арматуры и счётчиков — по всей квартире (К-17)<br>О-2: обмер: Спальня 1 (пом. 1), Спальня 2 (пом. 4), Кухня-гостиная (пом. 6); у окон | Санузел 2: ниша 1600 × 1840 мм у входа закрыта перегородкой, ниша 660 × 260 мм (уступ по плану) — фальш-стеной с рамой инсталляции: проектное решение, на плане заказчика ниша у входа открыта в кухню-гостиную. (К-18)<br>Вход в санузел 2 (с унитазом) — из кухни-гостиной: так по плану заказчика (ниша у входа на плане открыта в кухню-гостиную, в проекте закрыта перегородкой по линии низа прихожей). (К-4) | После 1 и 2 и после получения срока у поставщика (К-28); дата заказа — когда срок известен, не позднее чем за срок до начала Р-5. | срок уточняется у поставщика | Р-5 «черновая сантехника»: инсталляцию ставят до обшивки ГКЛВ и до гидроизоляции стены | К-4, К-17, К-18, К-28 |
| З-7 | Керамогранит и плитка: 4 поз. по артикулу и формату, 48,96 м² по раскладке<br>пом. 2, 5, 6, 7 | О-16: обмер: Спальня 1 (пом. 1), Ванная (пом. 2), Гардеробная (пом. 3), Спальня 2 (пом. 4), Прихожая (пом. 5), Кухня-гостиная (пом. 6), Санузел 2 (пом. 7), Коридор (пом. 8) | О-18: Артикул плитки и калибр партии (фактический размер плитки) для ванной и санузла 2. (К-2); до заказа плитки и раскладки<br>О-21: Артикулы изделий отделки: инженерная доска 14/4 мм (дуб натуральный, масло, 1-полосная); керамогранит пола ректифицированный под травертин, матовый, 600 × 600 × 9 мм (пом. (К-23); до заказа материалов | После 1 и 2 и после получения срока у поставщика (К-28); дата заказа — когда срок известен, не позднее чем за срок до начала Р-10. | срок уточняется у поставщика | Р-10 «плитка»: калибр партии измеряют до раскладки, раскладку пересчитывают до заказа | К-2, К-23, К-28 |
| З-8 | Покрытие пола (доска) и плинтус: пом. 1, 3, 4, 6, 8<br>пом. 1, 3, 4, 6, 8 | | О-21: Артикулы изделий отделки: инженерная доска 14/4 мм (дуб натуральный, масло, 1-полосная); керамогранит пола ректифицированный под травертин, матовый, 600 × 600 × 9 мм (пом. (К-23); до заказа материалов | После 1 и 2 и после получения срока у поставщика (К-28); дата заказа — когда срок известен, не позднее чем за срок до начала Р-13. | срок уточняется у поставщика | Р-13 «чистовые полы»: артикул и партия — до заказа; доску привозят к чистовым полам | К-23, К-28 |
| З-9 | Встроенная мебель по замеру цеха: С5, М16<br>пом. 1, 5 | О-6: обмер: Вся квартира, все помещения; обход по часовой стрелке от входа (К-13, К-18) | | После 1 и 2 и после получения срока у поставщика (К-28); дата заказа — когда срок известен, не позднее чем за срок до начала Р-16. | срок уточняется у поставщика<br>Ориентир практики (не срок поставщика): 4–8 нед. от замера | Р-16 «кухня и мебель»: цех замеряет по готовым стенам; производство 4–8 недель идёт параллельно с отделкой | К-13, К-18, К-28 |

**Допущения и предложения на листе**

Основа листа: размеры сняты со скана плана заказчика по размерным цепочкам, контрольный обмер на объекте не выполнялся (К-13); высота потолка 2700 мм принята: на плане заказчика не указана (К-11); толщины стен приняты: наружные 250 мм, перегородки 150 мм («на плане 85–190 мм) (К-13); разрешённая мощность 15 кВт принята по типовой квартире, технических условий нет (К-14); утолщение стены 190 × 1360 мм и элемент 1470 × 160 мм плана заказчика не определены (К-12); ниши санузла 2 закрыты перегородкой и фальш-стеной: проектное решение, на плане заказчика ниша у входа открыта (К-18); несущие стены не определены: до технического заключения все существующие стены считаются несущими (К-20); окна существующие и сохраняются; подоконная доска и глубина откосов не заданы — приняты, не замерены (К-27).

Знак «*» — принято, не замерено и не подтверждено (замерить на объекте): ИЗ-11, К-19: П4 — вертикальная загрузка 400 × 600 мм — условие закупки (решение автора, ИЗ-11); модель не выбрана, габарит сверить по паспорту; К-8: М14, П11; К-17: Ст К1-1, Ст В1-1, Ст К1-2, Ст В1-2.

Знак «**» — предложение проектировщика, заказчиком не утверждено (согласовать с заказчиком): ИЗ-5, К-8: М6, М15.

Открытые вопросы и конфликты по листу: К-28.

См. лист открытых вопросов (лист 6, записи К-8, К-11; лист 7, записи К-12–К-14, К-17–К-20; лист 8, записи К-27, К-28; лист 9, запись ИЗ-5; лист 10, запись ИЗ-11).

| Изм. | Кол.уч | Лист | № док. | Подп. | Дата | ГД-2026-003-АИ | | | |
|---|---|---|---|---|---|---|---|---|---|
| | | | | | | Трёхкомнатная квартира<br>Общая площадь 78,95* м² · * размеры со скана, не замерены (реестр — п. 6–11, К-13) | | | |
| Разраб. | | Кырпан А.С. | | | 05.10.26 | Дизайн-проект интерьера трёхкомнатной квартиры | Стадия | Лист | Листов |
| Пров. | | | | | | | РП | 18 | 94 |
| ГИП | | | | | | | | | |
| Н. контр. | | | | | | График закупок и работ. Лист 2 из 4<br>М 6м | Кырпан Александр Сергеевич | | |
| Утв. | | | | | | | | | |

выпуск 05.10.2026 № 6add39ab8d · стр. 20 из 137

# График закупок и работ. Лист 3 из 4

Что заказывать и когда не раньше чего: относительный порядок без дат; срок поставки — из данных или «уточняется у поставщика»

## Работы: порядок и что не даёт начать

| № | Работа (стадия технологической последовательности) | После | Что должно быть к началу: условия и закупки | Не начинать, пока открыто в реестре |
|---|---|---|---|---|
| Р-1 | Демонтаж покрытий, отделки стен и потолков, дверных блоков и приборов; конструкции, стены и перегородки не трогать до технического заключения (стадия 1) | | до начала: запрошены документы на дом и БТИ; контрольный обмер до демонтажа (что видно) сделан | К-20: Несущие стены не определены: проект дома и план БТИ в материалах объекта отсутствуют, тип и серия дома неизвестны, техническое заключение о несущих конструкциях не выполнялось. |
| Р-2 | Контрольный обмер на голых стенах и обследование (задание — лист «Задание на контрольный обмер») (стадия 2) | Р-1 | после снятия отделки: видны стояки, каналы, щиток, толщины стен; до заказа всего, что делают по размеру | К-12: Две конструкции плана заказчика не определены: утолщение стены 190 × 1360 мм в гардеробной у спальни 2 (вентблок или пилон) и элемент 1470 × 160 мм на линии простенка кухни-гостиной (пилон, балка или барная стойка). |
| Р-3 | Перегородки и фальш-стены ГКЛ: разметка, каркас, обшивка (стадия 3) | Р-2 | до начала: решение по нише санузла 2 принято автором; разметка по плану монтажа подписана; коробка скрытой двери — в каркас до обшивки<br>Закупки к началу: З-1 (двери скрытого монтажа) | К-4: Вход в санузел 2 (с унитазом) — из кухни-гостиной: так по плану заказчика (ниша у входа на плане открыта в кухню-гостиную, в проекте закрыта перегородкой по линии низа прихожей).<br>К-13: Размеры сняты со скана плана заказчика по размерным цепочкам, контрольный обмер на объекте не выполнялся; толщины стен приняты 250 мм (наружные) и 150 мм (перегородки), на плане 85–190 мм.<br>К-18: Санузел 2: ниша 1600 × 1840 мм у входа закрыта перегородкой, ниша 660 × 260 мм (уступ по плану) — фальш-стеной с рамой инсталляции: проектное решение, на плане заказчика ниша у входа открыта в кухню-гостиную.<br>К-20: Несущие стены не определены: проект дома и план БТИ в материалах объекта отсутствуют, тип и серия дома неизвестны, техническое заключение о несущих конструкциях не выполнялось.<br>К-25: Скрытые двери Д-2 (спальня 1 и спальня 2), Д-3 (ванная) и Д-4 (гардеробная) заданы размером проёма 800×2100 со скана плана заказчика; проёмы существующие, расширять их до технического заключения (К-20) нельзя. |
| Р-4 | Черновая электрика: штробы, короба, гофра, подрозетники, щит (стадия 4) | Р-2, Р-3 | до начала: план электрики с высотами утверждён; штробы в стенах — только после технического заключения; мебель расставлена | К-14: Разрешённая мощность 15 кВт принята по типовой квартире, технических условий в материалах объекта нет; расчётная мощность 11,8 кВт.<br>К-20: Несущие стены не определены: проект дома и план БТИ в материалах объекта отсутствуют, тип и серия дома неизвестны, техническое заключение о несущих конструкциях не выполнялось. |
| Р-5 | Черновая сантехника и вентиляция: разводка, выводы, инсталляции, короба стояков (стадия 5) | Р-2, Р-3 | до начала: положение стояков замерено; модели инсталляций и машины выбраны (габариты рамы, подводка); инсталляцию ставят до обшивки ГКЛВ и до гидроизоляции<br>Закупки к началу: З-5 (стиральная машина), З-6 (сантехника) | К-4: Вход в санузел 2 (с унитазом) — из кухни-гостиной: так по плану заказчика (ниша у входа на плане открыта в кухню-гостиную, в проекте закрыта перегородкой по линии низа прихожей).<br>К-17: Положение стояков условно, на объекте не замерено: стояки канализации и холодной воды — в коробе Ш1 248 × 459 в углу ванной и в стене-пилоне Ш2 270 мм между санузлом 2 и кухней (по плану заказчика).<br>К-18: Санузел 2: ниша 1600 × 1840 мм у входа закрыта перегородкой, ниша 660 × 260 мм (уступ по плану) — фальш-стеной с рамой инсталляции: проектное решение, на плане заказчика ниша у входа открыта в кухню-гостиную.<br>К-19: Модель стиральной машины П4* не выбрана. |
| Р-6 | Коробки скрытых дверей, затем штукатурка стен и откосов (стадия 6) | Р-3, Р-4, Р-5 | до начала: электрика и сантехника смонтированы, штробы заделаны; коробки скрытых дверей установлены до штукатурки (поэтому заказ дверей — раньше работы)<br>Закупки к началу: З-2 (двери скрытого монтажа) | К-13: Размеры сняты со скана плана заказчика по размерным цепочкам, контрольный обмер на объекте не выполнялся; толщины стен приняты 250 мм (наружные) и 150 мм (перегородки), на плане 85–190 мм.<br>К-18: Санузел 2: ниша 1600 × 1840 мм у входа закрыта перегородкой, ниша 660 × 260 мм (уступ по плану) — фальш-стеной с рамой инсталляции: проектное решение, на плане заказчика ниша у входа открыта в кухню-гостиную.<br>К-25: Скрытые двери Д-2 (спальня 1 и спальня 2), Д-3 (ванная) и Д-4 (гардеробная) заданы размером проёма 800×2100 со скана плана заказчика; проёмы существующие, расширять их до технического заключения (К-20) нельзя. |
| Р-7 | Стяжка пола и тёплый пол (стадия 7) | Р-6 | до начала: штукатурка сделана; трубы под стяжкой приняты; нивелировка плиты выполнена | |

**Допущения и предложения на листе**

Основа листа: размеры сняты со скана плана заказчика по размерным цепочкам, контрольный обмер на объекте не выполнялся (К-13); высота потолка 2700 мм принята: на плане заказчика не указана (К-11); толщины стен приняты: наружные 250 мм, перегородки 150 мм (на плане 85–190 мм) (К-13); разрешённая мощность 15 кВт принята по типовой квартире, технических условий нет (К-14); утолщение стены 190 × 1360 мм и элемент 1470 × 160 мм плана заказчика не определены (К-12); ниши санузла 2 закрыты перегородкой и фальш-стеной: проектное решение, на плане заказчика ниша у входа открыта (К-18); несущие стены не определены: до технического заключения все существующие стены считаются несущими (К-20); окна существующие и сохраняются; подоконная доска и глубина откосов не заданы — приняты, не замерены (К-27).

Знак «*» — принято, не замерено и не подтверждено (замерить на объекте): И3-11, К-19: П4 — вертикальная загрузка 400 × 600 мм — условие закупки (решение автора, И3-11); модель не выбрана, габарит сверить по паспорту.

Открытые вопросы и конфликты по листу: К-28.

См. лист открытых вопросов (лист 6, запись К-11; лист 7, записи К-12–К-14, К-18–К-20; лист 8, записи К-27, К-28; лист 10, запись И3-11).

| Изм. | Кол.уч | Лист | № док. | Подп. | Дата |
|---|---|---|---|---|---|
| Разраб. | | Кырпан А.С. | | | 05.10.26 |
| Пров. | | | | | |
| ГИП | | | | | |
| | | | | | |
| Н. контр. | | | | | |
| Утв. | | | | | |

**ГД-2026-003-АИ**

Трёхкомнатная квартира

Общая площадь 78,95* м² · * размеры со скана, не замерены (реестр — п. 6–11, К-13)

Дизайн-проект интерьера трёхкомнатной квартиры

| Стадия | Лист | Листов |
|---|---|---|
| РП | 19 | 94 |

**График закупок и работ. Лист 3 из 4**

М 6/м

**Кырпан Александр Сергеевич**

выпуск 05.10.2026 № 6add39ab8d · стр. 21 из 137

# График закупок и работ. Лист 4 из 4

Что заказывать и когда не раньше чего: относительный порядок без дат; срок поставки — из данных или «уточняется у поставщика»

## Работы: порядок и что не даёт начать (продолжение)

| № | Работа (стадия технологической последовательности) | После | Что должно быть к началу: условия и закупки | Не начинать, пока открыто в реестре |
|---|---|---|---|---|
| Р-8 | Гидроизоляция санузлов и тест проливом (стадия 8) | Р-7 | до начала: стяжка набрала прочность и сухая по инструкции гидроизоляции; выводы стоят на проектных отметках | |
| Р-9 | ГКЛ: короба инсталляции и стояков, ниши, потолки (стадия 9) | Р-4, Р-5 | до начала: черновые сети в зоне коробов приняты; закладные под тяжёлое и карнизы стоят; светильники выбраны (вырезы) | |
| Р-10 | Плитка и керамогранит: стены, затем пол; фартук (стадия 10) | Р-7, Р-8, Р-9 | до начала: гидроизоляция принята; плитка выбрана, калибр партии измерен, раскладка пересчитана и подписана<br>Закупки к началу: З-7 (плитка) | К-2: Артикул плитки и калибр партии (фактический размер плитки) для ванной и санузла 2 не заданы: раскладка рассчитана по номинальным размерам — пол 600 × 600 мм, стены 600 × 1200 мм.<br>К-23: Артикулы изделий отделки не выбраны. |
| Р-11 | Шпаклёвка стен и потолков под окраску (стадия 11) | Р-6, Р-9, Р-10 | до начала: плитка готова (грязные работы закончены); штукатурка и ГКЛ сухие | |
| Р-12 | Окраска стен, потолков, откосов (стадия 13) | Р-11 | до начала: шпаклёвка отшлифована и огрунтована; выкрасы утверждены, колеровка одной партией | |
| Р-13 | Чистовые полы: инженерная доска (стадия 14) | Р-10, Р-12 | до начала: влажность основания в норме, мокрые работы закончены; доска выбрана и привезена<br>Закупки к началу: З-8 (доска и плинтус) | К-23: Артикулы изделий отделки не выбраны. |
| Р-14 | Полотна межкомнатных дверей, плинтусы, пороги (стадия 15) | Р-12, Р-13 | до начала: чистовой пол уложен; полотна скрытых дверей — после чистовой отделки стен | |
| Р-15 | Чистовая электрика и сантехника: механизмы, светильники, смесители, приборы (стадия 16) | Р-12, Р-14 | до начала: отделка готова; механизмы, светильники и приборы выбраны и привезены | |
| Р-16 | Кухня, встроенная и корпусная мебель, бытовая техника (стадия 17) | Р-14, Р-15 | до начала: чистовая сантехника и электрика подведены к местам мебели; замер кухни снят по готовым стенам (после штукатурки или плитки, до чистового пола)<br>Закупки к началу: З-3 (кухонный гарнитур), З-4 (техника кухни), З-9 (мебель по замеру) | К-8: Проект кухни не утверждён заказчиком: выводы кухонной техники (мойка М7*, посудомоечная М14*, варочная панель и духовой шкаф М8*, вытяжка М15**, холодильник М6**) приняты по типовой расстановке техники.<br>К-13: Размеры сняты со скана плана заказчика по размерным цепочкам, контрольный обмер на объекте не выполнялся; толщины стен приняты 250 мм (наружные) и 150 мм (перегородки), на плане 85–190 мм.<br>К-18: Санузел 2: ниша 1600 × 1840 мм у входа закрыта перегородкой, ниша 660 × 260 мм (уступ по плану) — фальш-стеной с рамой инсталляции: проектное решение, на плане заказчика ниша у входа открыта в кухню-гостиную.<br>К-24: Модели встраиваемой техники кухни не выбраны: холодильник (М6**) и посудомоечная машина (М14*) заданы описанием «аналог по характеристикам» — без производителя, серии и кода. |
| Р-17 | Сдача: осмотр по чек-листу, дефектная ведомость, устранение замечаний (стадия 18) | Р-15, Р-16 | до начала: всё смонтировано; акты скрытых работ подписаны | |

## Примечания

1. Порядок работ — стадии технологической последовательности из 17 позиций, присутствующих в этом проекте (по строкам ведомости объёмов); остальные стадии таблицы knowledge/remont-tehnologiya.md в проекте не встречаются. Длительности работ не печатаются: их нет ни в данных, ни в нормах для этого объекта.
2. Типовые сроки — ориентир практики, не срок поставщика: скрытые двери — короб около 10 дн., полотно под покраску до 3 нед., шпон 4–5 нед., в среднем около 30 дн. (knowledge/workers/foreman.md, п. 2.4 (profil-doors)); кухня и корпусная мебель — 4–8 недель от замера (knowledge/remont-tehnologiya.md, разд. 2; knowledge/workers/foreman.md, п. 2.4). Заказ по ориентиру не назначается: срок получают у поставщика (вопрос реестра), после чего заказ планируют «не позднее чем за срок до начала работы».
3. Условия заказа берутся из реестра открытых вопросов и задания на контрольный обмер: позиция заказывается, когда закрыты замер (графа 1) и решение (графа 2). Закрывать их может только факт или решение автора с подписью; снять строку с листа можно только закрыв запись реестра.
4. Заказ по размеру до контрольного обмера не делают: двери, кухня и встроенная мебель зависят от обмера (К-11, К-13); скрытые двери, кроме того, зависят от решения по нише санузла 2 (проём Д-5 в перегородке П-1**).
5. Номера листов — по ведомости рабочих чертежей комплекта (лист «Общие данные»).

**Допущения и предложения на листе**

Основа листа: размеры сняты со скана плана заказчика по размерным цепочкам, контрольный обмер на объекте не выполнялся (К-13); высота потолка 2700 мм принята: на плане заказчика не указана (К-11); толщины стен приняты: наружные 250 мм, перегородки 150 мм (на плане 85–190 мм) (К-13); разрешённая мощность 15 кВт принята по типовой квартире, технических условий нет (К-14); утолщение стены 190 × 1360 мм и элемент 1470 × 160 мм плана заказчика не определены (К-12); ниши санузла 2 закрыты перегородкой и фальш-стеной: проектное решение, на плане заказчика ниша у входа открыта (К-18); несущие стены не определены: до технического заключения все существующие стены считаются несущими (К-20); окна существующие и сохраняются; подоконная доска и глубина откосов не заданы — приняты, не замерены (К-27).

Знак «*» — принято, не замерено и не подтверждено (замерить на объекте): К-8: М7, М14, М8.

Знак «**» — предложение проектировщика, заказчиком не утверждено (согласовать с заказчиком): ИЗ-5, К-8: М6, М15; К-4, К-18: П-1 — проектное решение исполнителя: на плане заказчика ниша у входа открыта в кухню-гостиную; конструкция не утверждена автором (вопрос К-18), положение и размеры сняты со скана (К-13).

Открытые вопросы и конфликты по листу: К-28.

См. лист открытых вопросов (лист 6, записи К-4, К-8, К-11; лист 7, записи К-12–К-14, К-18, К-20; лист 8, записи К-27, К-28; лист 9, запись ИЗ-5).

| Изм. | Кол.уч | Лист | № док. | Подп. | Дата | ГД-2026-003-АИ | | | |
|---|---|---|---|---|---|---|---|---|---|
| Разраб. | | Кырпан А.С. | | | 05.10.26 | Трёхкомнатная квартира<br>Общая площадь 78,95* м² · * размеры со скана, не замерены (реестр — п. 6–11, К-13) | | | |
| Пров. | | | | | | Дизайн-проект интерьера трёхкомнатной квартиры | Стадия | Лист | Листов |
| ГИП | | | | | | | РП | 20 | 94 |
| | | | | | | | | | |
| Н. контр. | | | | | | График закупок и работ. Лист 4 из 4<br>М 6/м | Кырпан Александр Сергеевич | | |
| Утв. | | | | | | | | | |

выпуск 05.10.2026 № 6add39ab8d · стр. 22 из 137

01

# Архитектурные решения

Кырлан Александр Сергеевич

выпуск 05.10.2026 № 6add39ab8d · стр. 23 из 137

# Обмерный план

Существующее положение · размеры в мм · отметки от чистого пола

ПРЕДВАРИТЕЛЬНО · не для производства работ · открыто пунктов: 31 (реестр — л. 6–11)

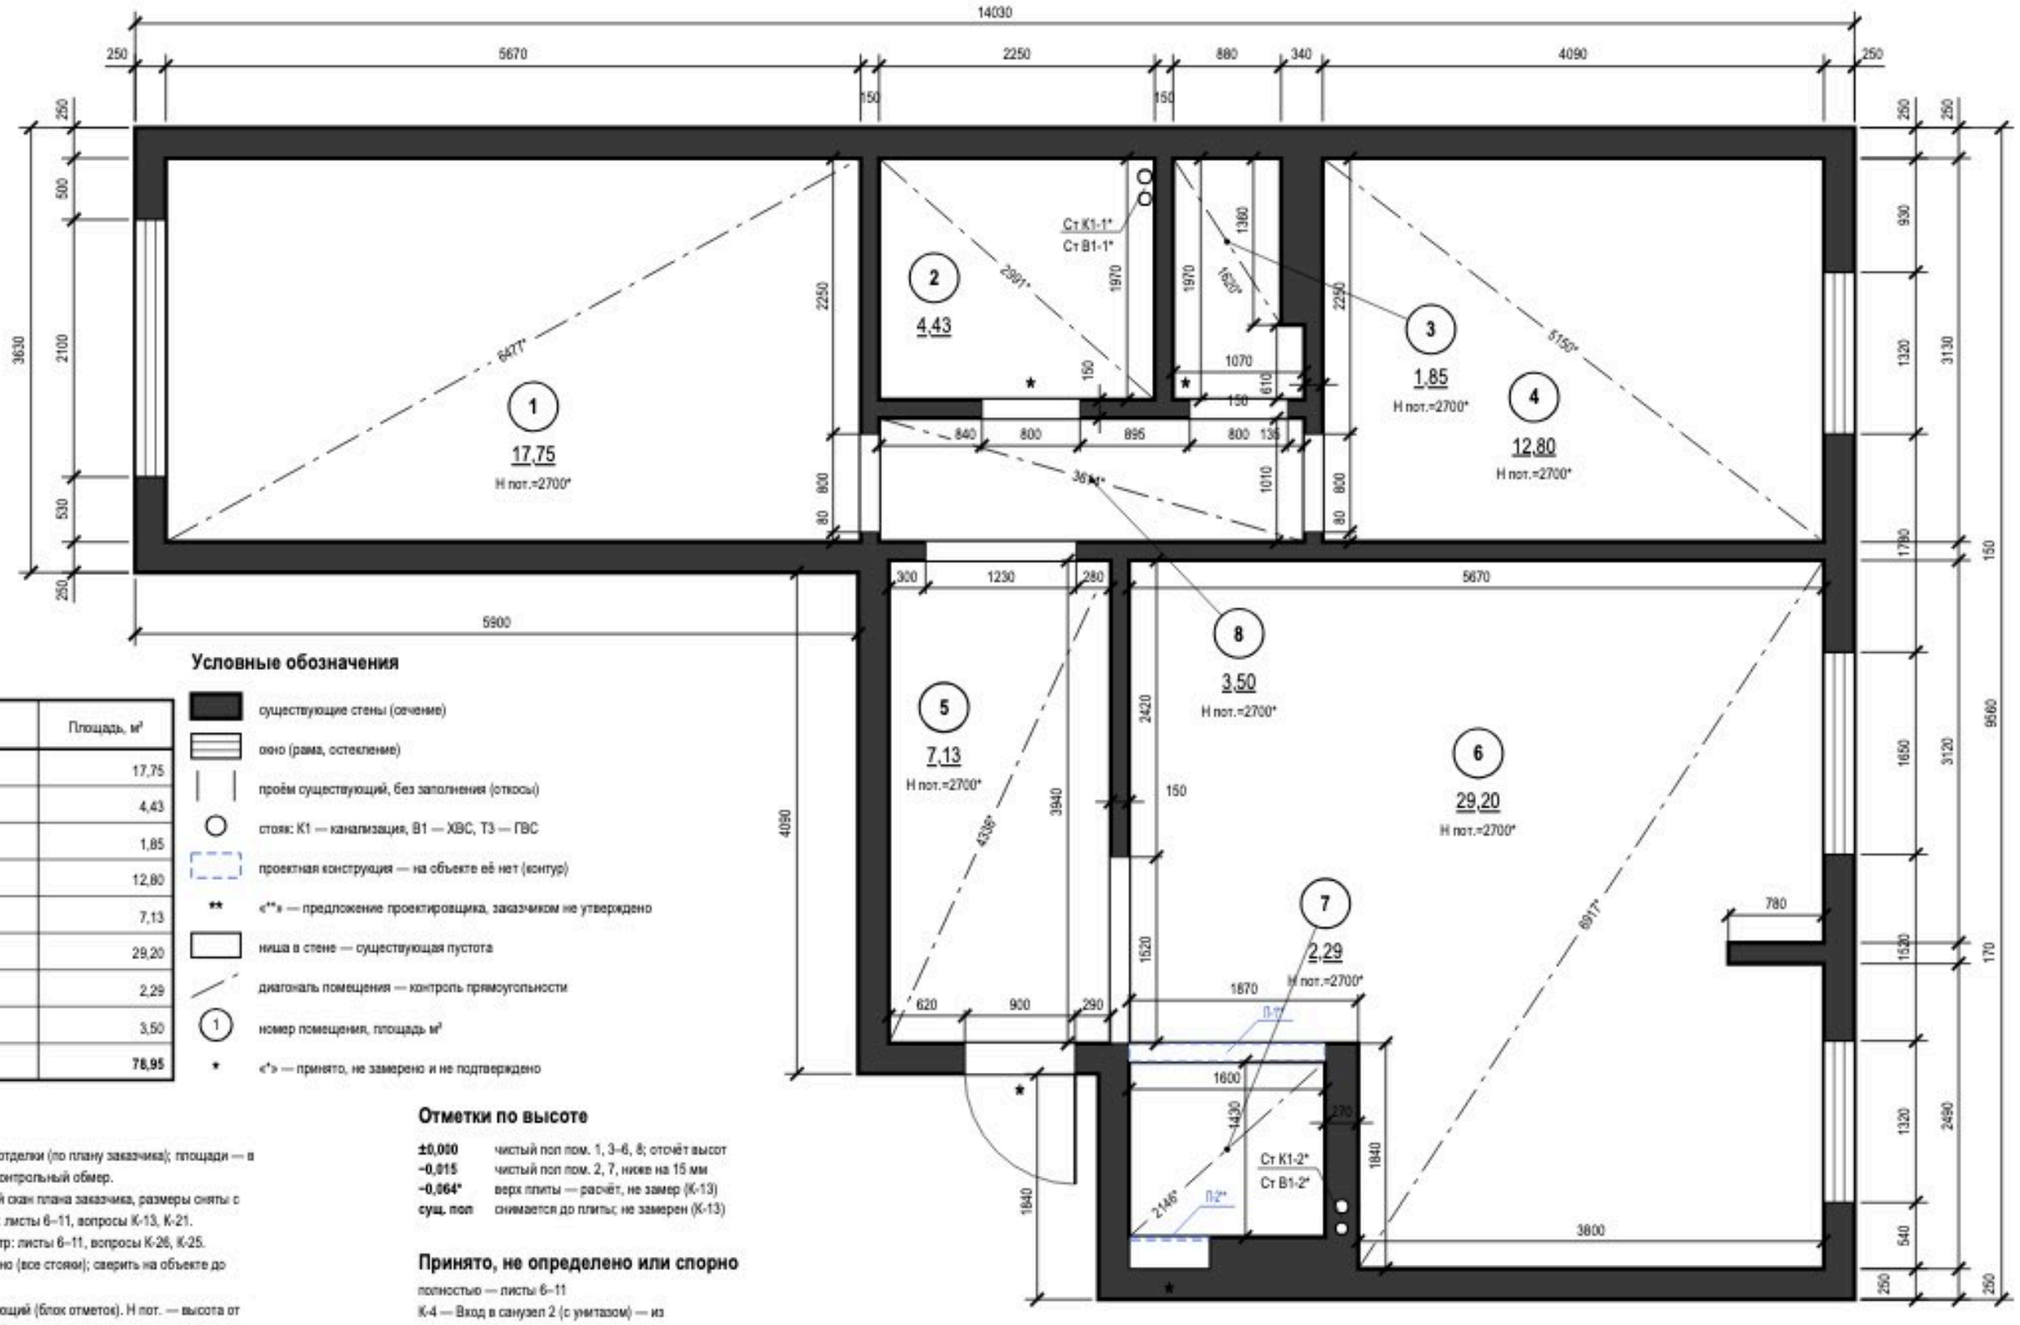


## Экспликация помещений

| № | Наименование | Площадь, м² |
|---|---|---|
| 1 | Спальня 1 | 17,75 |
| 2 | Ванная | 4,43 |
| 3 | Гардеробная | 1,85 |
| 4 | Спальня 2 | 12,80 |
| 5 | Прихожая | 7,13 |
| 6 | Кухня-гостиная | 29,20 |
| 7 | Санузел 2 | 2,29 |
| 8 | Коридор | 3,50 |
| | **Итого (общая площадь)** | **78,95** |

## Условные обозначения

- существующие стены (сечение)
- окно (рама, остекление)
- проём существующий, без заполнения (откосы)
- стояк: К1 — канализация, В1 — ХВС, Т3 — ГВС
- проектная конструкция — на объекте её нет (контур)
- «**» — предложение проектировщика, заказчиком не утверждено
- ниша в стене — существующая пустота
- диагональ помещения — контроль прямоугольности
- (1) номер помещения, площадь м²
- * «*» — принято, не замерено и не подтверждено

## Примечания

1. Размеры — в мм по чистым поверхностям стен до отделки (по плану заказчика); площади — в м² по тем же размерам. До начала работ выполнить контрольный обмер.
2. Источник плана — допущение, не замер: растровый скан плана заказчика, размеры сняты с размерных цепочек, на объекте не замерены. Реестр: листы 6–11, вопросы К-13, К-21.
3. Знак «*» у проёма — положение не замерено; реестр: листы 6–11, вопросы К-26, К-25.
4. Знак «*» у стояка — положение принято, не замерено (все стояки); сверить на объекте до разметки. Реестр: листы 6–11, вопрос К-17.
5. За отметку ±0,000 принят чистый пол, не существующий (блок отметок). Н пот. — высота от чистого пола до плиты перекрытия; Н пот. со знаком «*» — принятая высота, не замер (вопрос К-11).
6. Толщины стен: наружные 250 мм, перегородки 150 мм — приняты, не замерены (вопрос К-13); отличающиеся толщины и уступы — размерами на плане.
7. Несущие стены не определены: до технического заключения все стены считать несущими; проёмы и штробы в них не выполнять.
8. Дверные проёмы показаны без заполнения (двери — лист 24); высота дверных проёмов 2100 мм, проёмов без двери 2500, 2100 мм; низ окон (подоконник) 900 мм от чистого пола, высота окон 1500, 1400 мм.
9. Диагонали — контрольные размеры; «*» — расчёт по принятому контуру (К-13), при обмере заменить замеренным; расхождение более 5 мм подписать на плане как перекос.
10. Размеры проверить на месте до начала работ; расхождение контрольных промеров ≤ 2 %.

## Отметки по высоте

| | |
|---|---|
| **±0,000** | чистый пол пом. 1, 3–6, 8; отсчёт высот |
| **−0,015** | чистый пол пом. 2, 7, ниже на 15 мм |
| **−0,064*** | верх плиты — расчёт, не замер (К-13) |
| **сущ. пол** | снимается до плиты; не замерен (К-13) |

## Принято, не определено или спорно

полностью — листы 6–11

К-4 — Вход в санузел 2 (с унитазом) — из кухни-гостиной: так по плану заказчика (ниша у входа на плане открыта в кухню-гостиную, в проекте закрыта перегородкой по линии низа прихожей)

К-12 — Две конструкции плана заказчика не определены: утолщение стены 190 × 1360 мм в гардеробной у спальни 2 (вентблок или пилон) и элемент 1470 × 160 мм на линии простенка кухни-гостиной (пилон, балка или барная стойка)

Допущения и предложения на листе. Знак «*» принято (замерить): отметка существующего пола. Знак «**» предложено (согласовать). См. лист открытых вопросов (листы 6–11).

1000 мм · печать 1:1

| Изм. | Кол.уч | Лист | № док. | Подп. | Дата |
|---|---|---|---|---|---|
| Разраб. | | Кырпан А.С. | | | 05.10.26 |
| Пров. | | | | | |
| ГИП | | | | | |
| Н. контр. | | | | | |
| Утв. | | | | | |

**ГД-2026-003-АИ**

Трёхкомнатная квартира

Общая площадь 78,95* м² · * размеры со скана, не замерены (реестр — л. 6–11, К-13)

Дизайн-проект интерьера трёхкомнатной квартиры

| Стадия | Лист | Листов |
|---|---|---|
| РП | 21 | 94 |

**Обмерный план**

М 1:50

Кырпан Александр Сергеевич

выпуск 05.10.2026 · 6add39ab8d · стр. 24 из 137

# План демонтажа и монтажа перегородок

Существующее — серым, демонтаж — красным, монтаж — синим · размеры в мм

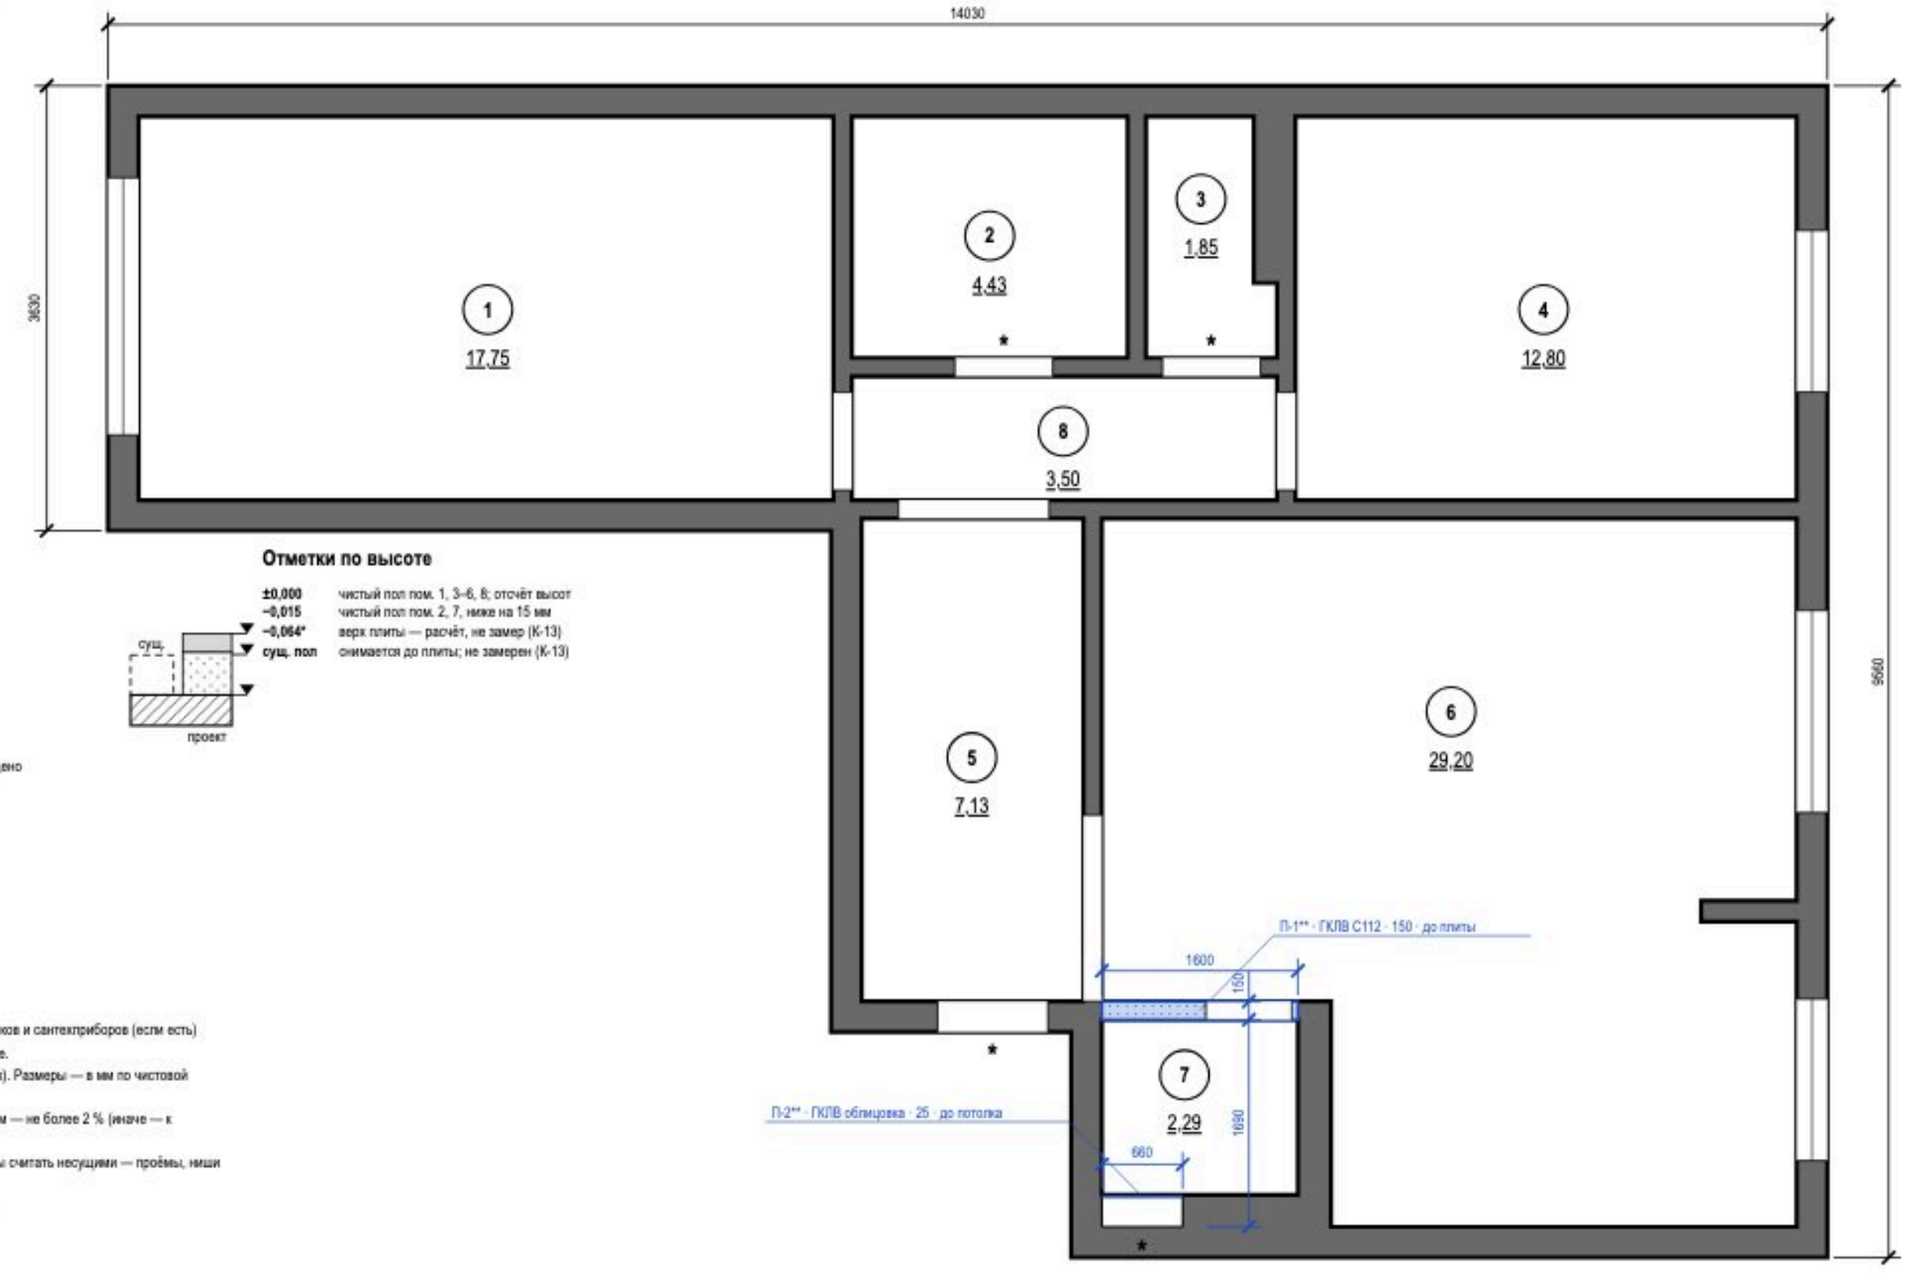


## Условные обозначения

- существующие стены — сохраняются;
- несущие не определены — считать несущими
- демонтируемые конструкции — на плане нет
- новое — возводится по проекту (синим)
- ** — «**» — предложение проектировщика, заказчиком не утверждено
- ниша в стене — существующая пустота
- проём существующий, без заполнения (откосы)
- (1) — номер помещения, площадь м²
- * — «*» — принято, не замерено и не подтверждено

## Отметки по высоте




| | |
|---|---|
| ±0,000 | чистый пол пом. 1, 3–6, 8; отсчёт высот |
| −0,015 | чистый пол пом. 2, 7, ниже на 15 мм |
| −0,064* | верх плиты — расчёт, не замер (К-13) |
| сущ. пол | снимается до плиты; не замерен (К-13) |

## Примечания

1. Демонтаж несущих стен и плит перекрытия не производится.
2. Демонтаж существующих покрытий пола, стен и потолка, дверных блоков и сантехприборов (если есть) — до основания; объёмы демонтажа — для справки, по факту на объекте.
3. За отметку ±0,000 принят чистый пол, не существующий (блок отметок). Размеры — в мм по чистовой поверхности стен до отделки.
4. Размеры проверить на месте до начала работ: расхождение с обмером — не более 2 % (иначе — к архитектору).
5. Несущие стены не определены: до технического заключения все стены считать несущими — проёмы, ниши и штробы в них не выполнять.
6. Ведомость демонтажа и монтажа и остальные примечания — лист 23.

Допущения и предложения на листе. Основа листа: размеры сняты со скана плана заказчика по размерным цепочкам, контрольный обмер на объекте не выполнялся (К-13); высота потолка 2700 мм принята: на плане заказчика не указана (К-11); толщины стен приняты: наружные 250 мм, перегородки 150 мм (на плане 85–190 мм) (К-13); разрешённая мощность 15 кВт принята по типовой квартире, технических условий нет (К-14); утолщение стены 190 × 1360 мм и элемент 1470 × 160 мм плана заказчика не определены (К-12); ниши санузла 2 закрыты перегородкой и фальш-стеной: проектное решение, на плане заказчика ниша у входа открыта (К-18); несущие стены не определены: до технического заключения все существующие стены считаются несущими (К-20); окна существующие и сохраняются; подоконная доска и глубина откосов не заданы — приняты, не замерены (К-27). Знак «*» — принято, не замерено и не подтверждено (замерить на объекте): К-13: отметка существующего пола — отметка существующего пола и верха плиты не замерена: на плане заказчика отметок нет; нивелировка — в задании на обмер (К-13). Знак «**» — предложение проектировщика, заказчиком не утверждено (согласовать с заказчиком): К-4, К-18: П-1 — проектное решение исполнителя: на плане заказчика ниша у входа открыта в кухню-гостиную; конструкция не утверждена автором (вопрос К-18), положение и размеры сняты со скана (К-13); К-18: П-2 — проектное решение исполнителя: на плане заказчика у наружной стены уступ 660 × 260 мм; конструкция не утверждена автором (вопрос К-18). См. лист открытых вопросов (лист 6, записи К-4, К-11; лист 7, записи К-12–К-14, К-18, К-20; лист 8, записи К-25–К-27); по листу — К-20.

1000 мм · печать 1:1

| Изм. | Кол.уч | Лист | № док. | Подп. | Дата |
|---|---|---|---|---|---|
| Разраб. | | Кырпан А.С. | | | 05.10.26 |
| Пров. | | | | | |
| ГИП | | | | | |
| | | | | | |
| Н. контр. | | | | | |
| Утв. | | | | | |

**ГД-2026-003-АИ**

Трёхкомнатная квартира

Общая площадь 78,95* м² · * размеры со скана, не замерены (реестр — п. 6–11, К-13)

Дизайн-проект интерьера трёхкомнатной квартиры

| Стадия | Лист | Листов |
|---|---|---|
| РП | 22 | 94 |

План демонтажа и монтажа перегородок

М 1:50

Кырпан Александр Сергеевич

выпуск 05.10.2026 · 6add39ab8d · стр. 25 из 137

# Ведомость демонтажа и монтажа перегородок

Демонтаж — красным, монтаж — синим (на плане) · размеры в мм

### Ведомость демонтажа и монтажа

| Марка | Конструкция | Длина, мм | Толщ., мм | Высота | Примечание |
|---|---|---|---|---|---|
| П-1* | монтаж: ГКЛВ 2 слоя с каждой стороны по металлическому каркасу ПС 100, С112 | 1600 | 150 | до плиты, 2700 | закрывает нишу 1600×1840; проём Д-5 700, обрамление УА; упор — наружная стена и пилон Ш2 |
| П-2* | монтаж: фальш-стена (облицовка), ГКЛВ 2 слоя по раме инсталляции унитаза; лицевая плоскость по линии уступа стены, без системы Knauf | 660 | 25 | до потолка, 2389 | закрывает нишу 660×260 у наружной стены; за ней рама инсталляции |

### Примечания

1. План демонтажа и монтажа в масштабе 1:50 — лист 22; марки в ведомости — те же, что на плане.
2. Демонтаж несущих стен и плит перекрытия не производится.
3. Новые перегородки и фальш-стены (синим) привязаны от капитальных стен и наружного контура; высота — по ведомости («до плиты» — до низа плиты перекрытия); проёмы в них усилить стойками каркаса.
4. Знак «*» — предложение проектировщика, заказчиком не утверждено (согласовать с заказчиком) у конструкций (вопросы К-18, К-4): до решения не возводить. На обмере они показаны контуром — на объекте их нет.
5. Перепланировку согласовать до начала работ (ЖК РФ, ст. 26); план не передавать в работу до допуска главного инженера проекта.
6. Дверные блоки — по плану дверей (лист 24); существующие проёмы не расширяются.
7. Знак «*» — положение проёма не замерено: двери пом. 5, 8, 8. Реестр: листы 6–11, вопросы К-26, К-25.
8. Демонтаж существующих покрытий пола, стен и потолка, дверных блоков и сантехприборов (если есть) — до основания; объёмы демонтажа — для справки, по факту на объекте.
9. За отметку ±0,000 принят чистый пол, не существующий (блок отметок). Размеры — в мм по чистовой поверхности стен до отделки.
10. Размеры проверить на месте до начала работ: расхождение с обмером — не более 2 % (иначе — к архитектору).
11. Несущие стены не определены: до технического заключения все стены считать несущими — проёмы, ниши и штробы в них не выполнять.

**Допущения и предложения на листе**

Основа листа: размеры сняты со скана плана заказчика по размерным цепочкам, контрольный обмер на объекте не выполнялся (К-13); высота потолка 2700 мм принята: на плане заказчика не указана (К-11); толщины стен приняты: наружные 250 мм, перегородки 150 мм (на плане 85–190 мм) (К-13); разрешённая мощность 15 кВт принята по типовой квартире, технических условий нет (К-14); утолщение стены 190 × 1360 мм и элемент 1470 × 160 мм плана заказчика не определены (К-12); ниши санузла 2 закрыты перегородкой и фальш-стеной: проектное решение, на плане заказчика ниша у входа открыта (К-18); несущие стены не определены: до технического заключения все существующие стены считаются несущими (К-20); окна существующие и сохраняются; подоконная доска и глубина откосов не заданы — приняты, не замерены (К-27).

Знак «*» — предложение проектировщика, заказчиком не утверждено (согласовать с заказчиком): К-4, К-18: П-1 — проектное решение исполнителя: на плане заказчика ниша у входа открыта в кухню-гостиную; конструкция не утверждена автором (вопрос К-18), положение и размеры сняты со скана (К-13); К-18: П-2 — проектное решение исполнителя: на плане заказчика у наружной стены уступ 660 × 260 мм; конструкция не утверждена автором (вопрос К-18).

См. лист открытых вопросов (лист 6, записи К-4, К-11; лист 7, записи К-12–К-14, К-18, К-20; лист 8, запись К-27).

| | | | | | | | | |
|---|---|---|---|---|---|---|---|---|
| | | | | | | **ГД-2026-003-АИ** | | |
| | | | | | | Трёхкомнатная квартира | | |
| | | | | | | Общая площадь 78,95* м² · * размеры со скана, не замерены (реестр — л. 6–11, К-13) | | |
| Изм. | Кол.уч | Лист | № док. | Подп. | Дата | | | |
| Разраб. | | Кырлан А.С. | | | 05.10.26 | Дизайн-проект интерьера трёхкомнатной квартиры | Стадия: РП | Лист: 23 / Листов: 94 |
| Пров. | | | | | | | | |
| ГИП | | | | | | | | |
| | | | | | | **Ведомость демонтажа и монтажа перегородок** М 6/м | **Кырлан Александр Сергеевич** | |
| Н. контр. | | | | | | | | |
| Утв. | | | | | | | | |

выпуск 05.10.2026 · 6add39ab8d · стр. 26 из 137

# План дверей и ведомость заполнения проёмов

Проёмы, марки заполнения, привязки · размеры в мм

## Условные обозначения

- стены (подложка обмера)
- новое — возводится по проекту (синим)
- дверь распашная, дуга открывания
- дверь скрытого монтажа
- дверь входная (полотно толще)
- портал (штрих — перемычка)
- оконный блок
- Д — марка типа (Д-N, ПР-N, ОК-N)
- 1 — номер помещения, площадь м²
- * — «*» — принято, не замерено и не подтверждено

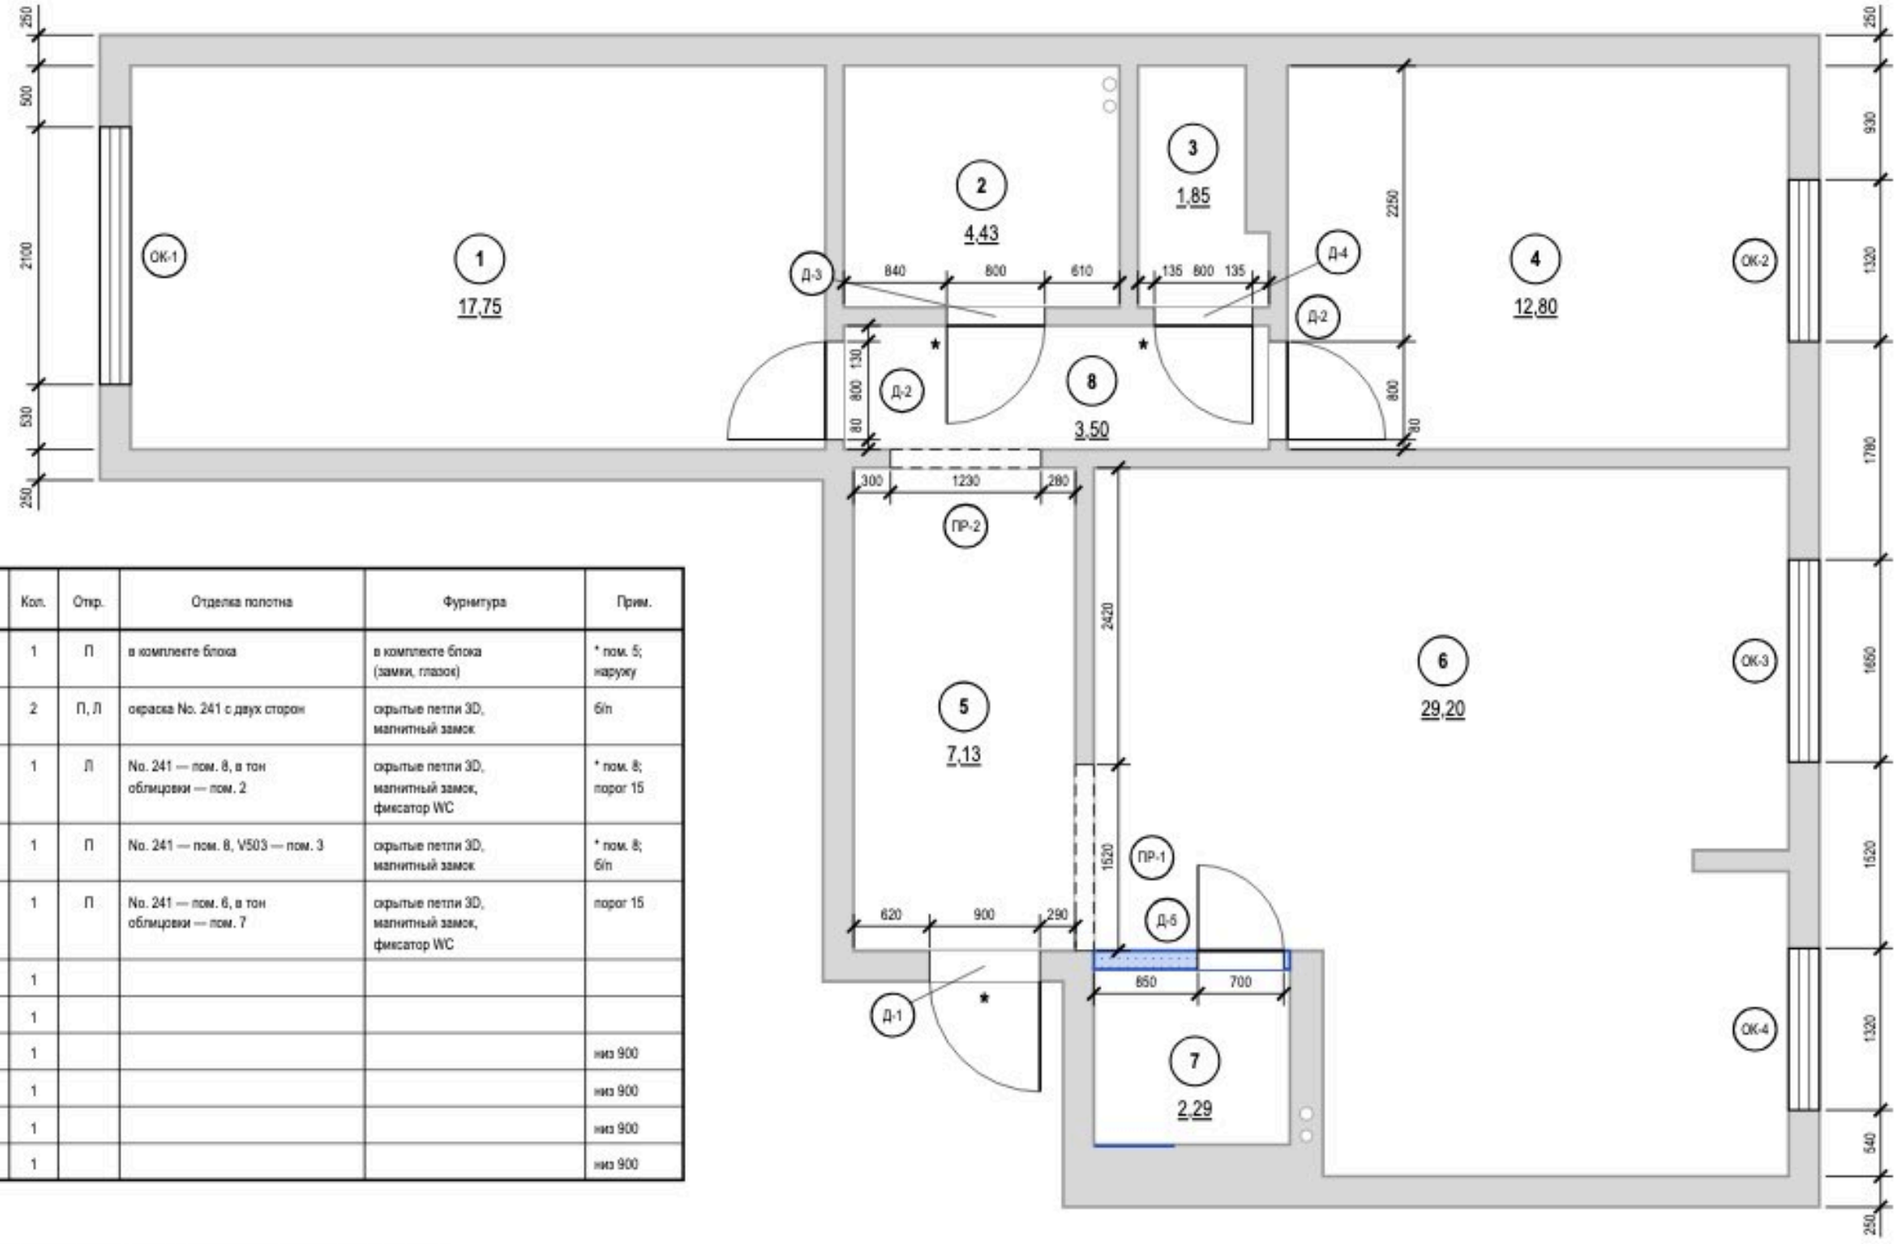


## Ведомость заполнения проёмов

| Марка | Наименование, обозначение | Проём ш×в, мм | Кол. | Откр. | Отделка полотна | Фурнитура | Прим. |
|---|---|---|---|---|---|---|---|
| Д-1 | Блок дверной входной, ГОСТ 31173-2016 | 900×2100 | 1 | П | в комплекте блока | в комплекте блока (замки, глазок) | * пом. 5; наружу |
| Д-2 | Дверь скрытого монтажа, ТУ изготовителя | 800×2100 | 2 | П, Л | окраска No. 241 с двух сторон | скрытые петли 3D, магнитный замок | б/п |
| Д-3 | Дверь скрытого монтажа, ТУ изготовителя | 800×2100 | 1 | Л | No. 241 — пом. 8, в тон облицовки — пом. 2 | скрытые петли 3D, магнитный замок, фиксатор WC | * пом. 8; порог 15 |
| Д-4 | Дверь скрытого монтажа, ТУ изготовителя | 800×2100 | 1 | П | No. 241 — пом. 8, V503 — пом. 3 | скрытые петли 3D, магнитный замок | * пом. 8; б/п |
| Д-5 | Дверь скрытого монтажа, ТУ изготовителя | 700×2100 | 1 | П | No. 241 — пом. 6, в тон облицовки — пом. 7 | скрытые петли 3D, магнитный замок, фиксатор WC | порог 15 |
| ПР-1 | Портал без заполнения | 1520×2500 | 1 | | | | |
| ПР-2 | Портал без заполнения | 1230×2100 | 1 | | | | |
| ОК-1 | Блок оконный существующий | 2100×1500 | 1 | | | | низ 900 |
| ОК-2 | Блок оконный существующий | 1320×1500 | 1 | | | | низ 900 |
| ОК-3 | Блок оконный существующий | 1650×1500 | 1 | | | | низ 900 |
| ОК-4 | Блок оконный существующий | 1320×1400 | 1 | | | | низ 900 |

## Примечания

1. Размеры проёмов и привязки — в миллиметрах от чистых граней стен до отделки; привязка — от угла того помещения, со стороны которого стоит размер. Размер в ведомости — ширина × высота проёма от чистого пола 0,000. Откос от угла помещения до проёма с коробкой — не менее 50 мм.
2. Марки в кружках — типы заполнения проёмов (ГОСТ 21.501-2018, п. 5.3.2); одна марка — один типоразмер; количество сверено с планом.
3. Открывание: Л — петли слева, П — справа, если смотреть со стороны, куда открывается полотно (на себя).
4. Скрытые двери (Д-2…Д-5): проём замерить в чистоте; блок заказать до штукатурки (≈ 30 дн.), короб ставить до штукатурки; полотно навесить после чистовой отделки, красить в цвет стен. Порядок — практика монтажа, изготовитель подтверждает.
5. Размер в ведомости — проёма: полотно скрытой двери уже проёма на коробку и зазор 10–15 мм (модель не выбрана); Д-2…Д-4 — существующие проёмы, до техзаключения не расширять. Д-3, Д-4: стена принята 150 мм, по скану 85 мм, не замерено; узел — для 150 мм (К-25).
6. Д-1: дуга наружу — по плану заказчика, не проверено; блок оставить или заменить — не решено (К-26). Окна ОК-1…ОК-4 существующие, сохраняются; подоконники и откосы не заданы — приняты (К-27).
7. Размеры проёмов и привязки сняты со скана плана заказчика и на объекте не замерены (обмерный план — лист 21).
8. Знак «*» у проёма — допущение: положение проёма не замерено (дверь пом. 5, стена В; дверь пом. 8, стена А (2 шт.)); размер напечатан как принятый; в ведомости — знак «*» в графе «Прим.». Реестр: листы 6–11, вопросы К-26, К-25.
9. Экспликация помещений — лист 21; в марках помещений — номер и площадь, м².
10. Привязка проёма к углу помещения меньше 1 мм на листе, размер на плане не показан: Д-5 — 50 мм.

1000 мм · печать 1:1

Допущения и предложения на листе. Знак «*» принято (замерить): Ст К1-1, Ст В1-1, Ст К1-2, Ст В1-2. Знак «**» предложено (согласовать): П-1, П-2. См. лист открытых вопросов (листы 6–11).

| Изм. | Кол.уч | Лист | № док. | Подп. | Дата |
|---|---|---|---|---|---|
| Разраб. | | Кырпан А.С. | | | 05.10.26 |
| Пров. | | | | | |
| ГИП | | | | | |
| Н. контр. | | | | | |
| Утв. | | | | | |

**ГД-2026-003-АИ**

Трёхкомнатная квартира

Общая площадь 78,95* м² · * размеры со скана, не замерены (реестр — п. 6–11, К-13)

Дизайн-проект интерьера трёхкомнатной квартиры

| Стадия | Лист | Листов |
|---|---|---|
| РП | 24 | 94 |

План дверей и ведомость заполнения проёмов

М 1:50

Кырпан Александр Сергеевич

выпуск 05.10.2026 № 6add3ab8d · стр. 27 из 137

02

# Планировочное решение



выпуск 05.10.2026 № 6add39ab8d · стр. 28 из 137

# Концепция интерьера

Современный (контемпорари) · схема аналоговая · 60/30/10 · материалы, образы и зонирование

## Идея

Стиль — современный (контемпорари), тёплая редакция (warm contemporary): актуальность, комфорт, мягкая геометрия, контраст фактур, открытость, уверенность. Потолки V503, стены Skimming Stone No. 241, грейж H487 в текстиле, один глубокий акцент Hague Blue No. 30 (изголовья спален, ТВ-стена). Цветовая схема — аналоговая, пропорция 60/30/10: база на стенах и потолках, вторичный цвет — в текстиле и мягкой мебели, акцент — точечно.

## Мудборд: материалы и фактуры

Инженерная доска, дуб натуральный
пол

Керамогранит ректифицированный под травертин
пол

Winter · Tikkurila V503
потолок, стены, плинтус

Skimming Stone · Farrow & Ball No. 241
стены, плинтус

Hague Blue · Farrow & Ball No. 30
акцент (стена А)

Лён, Tikkurila H487
портьеры-волна, подушки декоративные на кровать

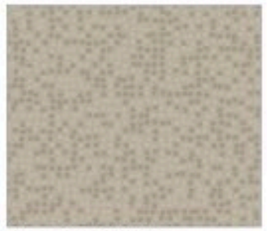

Шерсть, NCS S 3005-Y20R
ковёр под кроватью

Бархат, Farrow & Ball No. 30
подушки на кровать, подушки на диван

Букле, Farrow & Ball No. 229
подушки декоративные на кровать

## Палитра 60/30/10

60 % база — Tikkurila V503 Winter, LRV 86; Farrow & Ball No. 241 Skimming Stone, LRV 67

30 % вторичный — Tikkurila H487 Pumice, LRV 57

10 % акцент — Farrow & Ball No. 30 Hague Blue, LRV 7

## Свет

Цветовая температура 2700–3000 K (диапазон стиля 2700–3000 K); CRI не ниже 90; сценарии: вечер, уборка, ужин, кино, готовка. Общий свет — споты с диммированием, акцент — скрытая линейная подсветка, у кроватей — бра.

## Функциональное зонирование (М 1:200)

- дневная зона: гостиная, кухня, столовая
- мокрая зона: санузлы
- вход и коммуникации
- (1) номер помещения (лист 26)
- ночная зона: спальни
- хранение: гардеробная, кладовая
- функциональная зона в помещении

## Образы помещений

**6. Кухня-гостиная** — 29,20 м²

стены Farrow & Ball No. 241; акцент No. 30 на стене А
пол — доска, дуб натуральный
текстиль: портьеры H487, тюль V503, римская штора V484, ковёр в зоне отдыха V484

**1. Спальня 1** — 17,75 м²

стены Farrow & Ball No. 241; акцент No. 30 на стене А
пол — доска, дуб натуральный
текстиль: портьеры H487, тюль V503, ковёр S 3005-Y20R

**4. Спальня 2** — 12,80 м²

стены Farrow & Ball No. 241; акцент No. 30 на стене А
пол — доска, дуб натуральный
текстиль: портьеры H487, тюль V503, ковёр V484
декор: картина над кроватью, зеркало в рост

**5. Прихожая** — 7,13 м²

стены Farrow & Ball No. 241
пол — керамогранит под травертин, матовый
декор: зеркало
свет 3000/2700 K

**8. Коридор** — 3,50 м²

стены Farrow & Ball No. 241
пол — доска, дуб натуральный
свет 3000 K

**3. Гардеробная** — 1,85 м²

стены Tikkurila V503
пол — доска, дуб натуральный
свет 3000 K

**2. Ванная** — 4,43 м²

стены — керамогранит под травертин
пол — керамогранит под травертин, матовый
декор: зеркало над умывальником
свет 3000 K

**7. Санузел 2** — 2,29 м²

стены — керамогранит под травертин
пол — керамогранит под травертин, матовый
декор: зеркало над умывальником
свет 3000 K

## Материалы и отделка

**Инженерная доска, дуб натуральный**
масло, 1-полосная, 14/4 мм
пол — пом. 1, 3, 4, 6, 8

**Керамогранит ректифицированный под травертин**
матовый; 600×600, 600×1200
пол — пом. 2, 5, 7

**Керамогранит под травертин**
матовый; 600×1200, 1200×600
стены, фартук — пом. 2, 6, 7

**Farrow & Ball No. 241 Skimming Stone, LRV 67**
Farrow & Ball Modern Emulsion, матовая
стены, плинтус — пом. 1, 4, 5, 6, 8

**Tikkurila V503 Winter, LRV 86**
Tikkurila Anti-Reflex 2, глубокоматовая
потолок, стены, плинтус — пом. 1, 2, 3, 4, 5, 6, 7, 8

**Farrow & Ball No. 30 Hague Blue, LRV 7**
акцентная стена
акцент (стена А) — пом. 1, 4, 6

## Текстиль и металл

**Лён, Tikkurila H487**
портьеры-волна, подушки декоративные на кровать

**Шерсть, NCS S 3005-Y20R**
ковёр под кроватью

**Шерсть, Farrow & Ball No. 30**
плед на кровать

**Букле, Farrow & Ball No. 229**
подушки декоративные на кровать

**Чёрный матовый металл**
зеркало в рост, зеркало

**Вуаль, Tikkurila V503**
тюль

**Бархат, Farrow & Ball No. 30**
подушки на кровать, подушки на диван

**Шерсть, Tikkurila V484**
ковёр под кроватью, ковёр в зоне отдыха

**Бархат, Farrow & Ball No. 47**
подушки на кровать

**Лён, Tikkurila V484**
римская штора

## Чего избегаем

1) Смешение трёх и более металлов в одной комнате
2) Мебель из каталога всё сразу одной коллекции — теряется слоистость
3) Тренды без базы: весь интерьер на букле и арках к 2027 устареет
4) Глянцевый натяжной потолок и хромированные хай-тек детали 2000-х
5) Перегрузка акцентами разного цвета (синий + зелёный + терракота в одной комнате)
6) Холодный свет 4000 K в жилых зонах

**Допущения и предложения на листе**

Основа листа: размеры сняты со скана плана заказчика по размерным цепочкам, контрольный обмер на объекте не выполнялся (К-13); высота потолка 2700 мм принята: на плане заказчика не указана (К-11); толщины стен приняты: наружные 250 мм, перегородки 150 мм (на плане 85–190 мм) (К-13); разрешённая мощность 15 кВт принята по типовой квартире, технических условий нет (К-14); утолщение стены 190 × 1360 мм и элемент 1470 × 160 мм плана заказчика не определены (К-12); ниши санузла 2 закрыты перегородкой и фальш-стеной: проектное решение, на плане заказчика ниша у входа открыта (К-18); несущие стены не определены: до технического заключения все существующие стены считаются несущими (К-20); окна существующие и сохраняются; подоконная доска и глубина откосов не заданы — приняты, не замерены (К-27).

## Примечания

См. лист открытых вопросов (лист 6, запись К-11; лист 7, записи К-12–К-14, К-18, К-20; лист 8, запись К-27).

1. Коды цвета — по веерам производителей (колерная карта, лист 52); перед закупкой краски — выкрас на стене объекта под дневным светом и лампами проекта.
2. Материалы — по ведомости отделки (лист 51); мебель, текстиль и декор — по спецификации (лист 27). Образцы доски, керамогранита и тканей утвердить до заказа.
3. Фактуры на листе условные, цвет передан по HEX-значениям производителей: при печати возможны отклонения, решение — только по физическому образцу.

| | | | | | | | |
|---|---|---|---|---|---|---|---|
| | | | | | | ГД-2026-003-АИ | |
| | | | | | | Трёхкомнатная квартира | |
| | | | | | | Общая площадь 78,95* м² · * размеры со скана, не замерены (реестр — п. 6–11, К-13) | |
| Изм. | Кол.уч | Лист | № док. | Подп. | Дата | Дизайн-проект интерьера трёхкомнатной квартиры | Стадия: РП; Лист: 25; Листов: 94 |
| Разраб. | | Кырпан А.С. | | | 05.10.26 | | |
| Пров. | | | | | | | |
| ГИП | | | | | | | |
| Н. контр. | | | | | | Концепция интерьера — М б/м | Кырпан Александр Сергеевич |
| Утв. | | | | | | | |

выпуск 05.10.2026 № 6add39ab8d · стр. 29 из 137

# План расстановки мебели

Мебель и оборудование · размеры в мм от чистовых стен · марки — по ведомости

ПРЕДВАРИТЕЛЬНО · не для производства работ · открыто пунктов: 31 (реестр — л. 6–11)

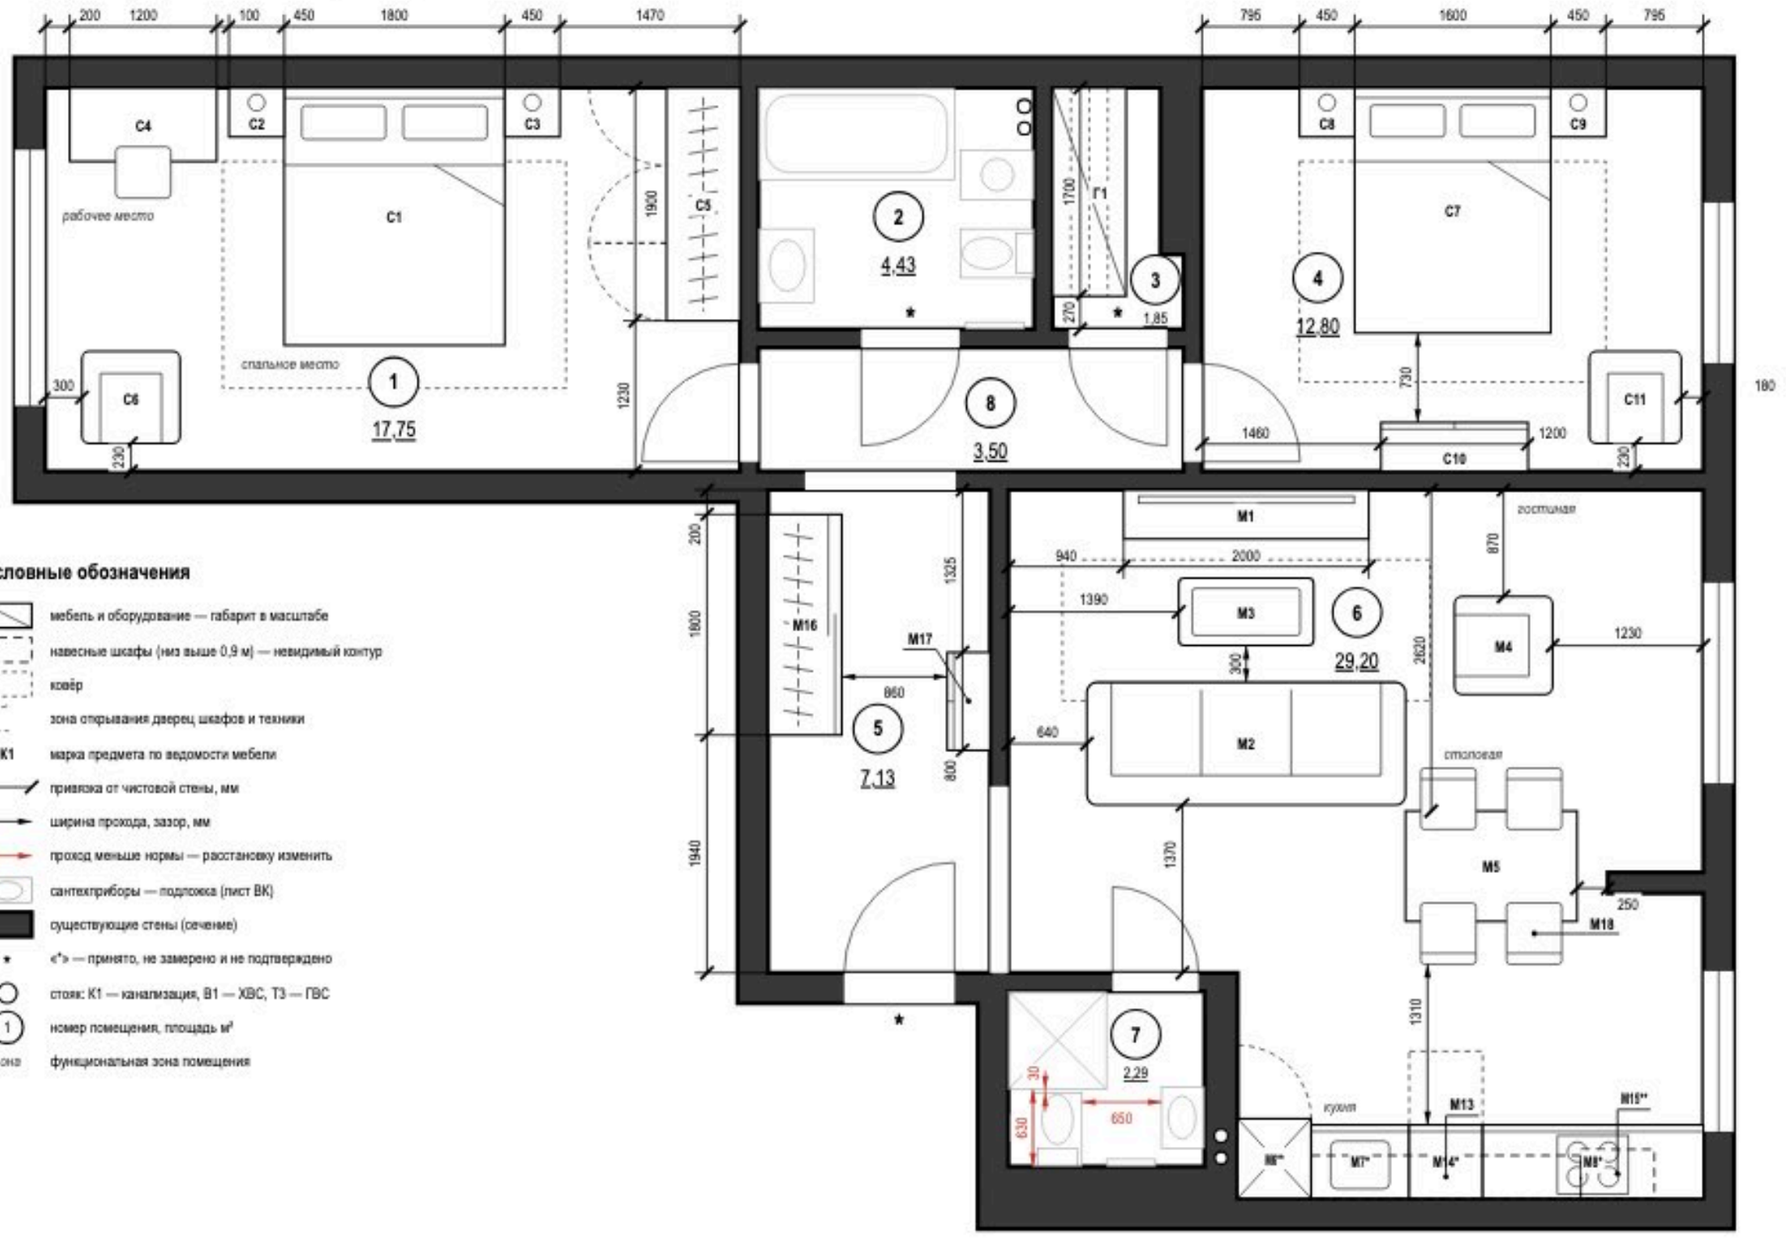


## Условные обозначения

- мебель и оборудование — габарит в масштабе
- навесные шкафы (низ выше 0,9 м) — невидимый контур
- ковёр
- зона открывания дверец шкафов и техники
- K1 — марка предмета по ведомости мебели
- привязка от чистовой стены, мм
- ширина прохода, зазор, мм
- проход меньше нормы — расстановку изменить
- сантехприборы — подложка (лист ВК)
- существующие стены (сечение)
- «*» — принято, не замерено и не подтверждено
- стояк: К1 — канализация, В1 — ХВС, Т3 — ГВС
- 1 — номер помещения, площадь м²
- зона — функциональная зона помещения

**Экспликация помещений**

лист 21 · на плане — номера в марках

## Ведомость мебели и оборудования

| Марка | Наименование | Ш×Г×В, мм | Пом. | Кол. |
|---|---|---|---|---|
| C1 | Кровать двуспальная | 1800×2100×450 | 1 | 1 |
| C2 | Тумба прикроватная | 450×400×550 | 1 | 1 |
| C3 | Тумба прикроватная | 450×400×550 | 1 | 1 |
| C4 | Стол письменный | 1200×600×750 | 1 | 1 |
| C5 | Шкаф распашной | 1900×600×2400 | 1 | 1 |
| C6 | Кресло | 800×750×800 | 1 | 1 |
| Г1 | Система хранения | 1700×600×2400 | 3 | 1 |
| C7 | Кровать двуспальная | 1600×2000×450 | 4 | 1 |
| C8 | Тумба прикроватная | 450×400×550 | 4 | 1 |
| C9 | Тумба прикроватная | 450×400×550 | 4 | 1 |
| C10 | Комод | 1200×400×850 | 4 | 1 |
| C11 | Кресло для чтения у окна | 750×750×800 | 4 | 1 |
| M16 | Шкаф-купе | 1800×600×2600 | 5 | 1 |
| M17 | Банкетка-обувница с мягким сиденьем | 800×350×450 | 5 | 1 |
| M1 | ТВ-тумба с экраном | 2000×400×500 | 6 | 1 |
| M2 | Диван | 2600×1000×800 | 6 | 1 |
| M3 | Стол журнальный | 1100×550×400 | 6 | 1 |
| M4 | Кресло | 800×800×800 | 6 | 1 |
| M5 | Стол обеденный | 1400×900×750 | 6 | 1 |
| M6* | Пенал кухонный | 600×650×2100 | 6 | 1 |
| M8* | Модуль нижний с мойкой | 800×600×900 | 6 | 1 |
| M14* | Модуль под встраиваемую посудомоечную | 600×600×900 | 6 | 1 |
| M8* | Модуль нижний | 1800×600×900 | 6 | 1 |
| M13 | Навесные шкафы | 2200×350×720 | 6 | 1 |
| M15** | Вытяжка над варочной панелью | 600×400×600 | 6 | 1 |
| M18 | Стул обеденный к столу M5 | 450×500×820 | 6 | 4 |

Ш — вдоль стены (изголовья), Г — от стены (длина кровати)

Материалы, модели, допуск замены — лист 27

## Примечания

1. Размеры даны в мм от чистовых поверхностей стен: слой штукатурки 20 мм по блоку и 5 мм шпаклёвки по ГКЛ учтён. Перед заказом встроенной мебели — контрольный обмер после штукатурки.
2. Привязки мебели — от стен и углов помещения, а не от другой мебели; ширина проходов и зазоров показана стрелками.
3. Розетки, выводы и выключатели под мебель — см. лист 29 «План розеток и электровыводов»; сантехприборы и выводы воды лист 39.
4. План расстановки не является документацией для изготовления мебели: изделия — по чертежам мебельщика; покупную мебель заменять только на изделия не больше габарита из спецификации (лист 27).
5. Встроенная мебель «стена в стену» — с зазором 10 мм с каждой стороны или с компенсаторами.
6. Знак «*» у проёма — допущение: положение проёма не замерено (дверь пом. 5, стена В; дверь пом. 8, стена А (2 шт.)); размер напечатан как принятый. Реестр: листы 6–11, вопросы К-26, К-25.
7. Стулья обеденной группы (M18 — 4 шт.) показаны в рабочем положении, задвинутыми под столешницу на 150 мм.

Допущения и предложения на листе. Знак «*» принято (замерить): Ст К1-1, Ст В1-1, Ст К1-2, Ст В1-2. Знак «**» предложено (согласовать). См. лист открытых вопросов (листы 6–11).

1000 мм · печать 1:1

| Изм. | Кол.уч | Лист | № док. | Подп. | Дата |
|---|---|---|---|---|---|
| Разраб. | | Кырпан А.С. | | | 05.10.26 |
| Пров. | | | | | |
| ГИП | | | | | |
| | | | | | |
| Н. контр. | | | | | |
| Утв. | | | | | |

**ГД-2026-003-АИ**

Трёхкомнатная квартира

Общая площадь 78,95* м² · * размеры со скана, не замерены (реестр — п. 6–11, К-13)

Дизайн-проект интерьера трёхкомнатной квартиры

| Стадия | Лист | Листов |
|---|---|---|
| РП | 26 | 94 |

**План расстановки мебели**

М 1:50

Кырпан Александр Сергеевич

выпуск 05.10.2026 · 6add39ab8d · стр. 30 из 137

# Спецификация мебели и оборудования

ПРЕДВАРИТЕЛЬНО · не для производства работ · открыто пунктов: 31 (реестр — л. 6–11)

Форма 1 ГОСТ 21.110-2013 · позиции мебели — по плану расстановки

| Поз. | Наименование и техническая характеристика | Тип, марка, обозначение документа, опросного листа | Код продукции | Поставщик | Ед. измерения | Кол. | Масса 1 ед., кг | Примечание |
|---|---|---|---|---|---|---|---|---|
| | **Мебель встроенная и корпусная (изготовление по чертежам мебельщика)** | | | | | | | |
| С5 | Шкаф распашной; корпус ЛДСП, фасады — матовая эмаль в цвет стен (Farrow & Ball No. 241); Ш×Г×В 1900×600×2400 мм | | | изготовление на заказ | шт. | 1 | | пом. 1; крепление к стене |
| Г1 | Система хранения: штанги, полки, ящики; каркас и полки — ЛДСП, декор «дуб натуральный»; Ш×Г×В 1700×600×2400 мм | | | изготовление на заказ | шт. | 1 | | пом. 3; крепление к стене |
| М16 | Шкаф-купе; корпус ЛДСП, фасады — матовая эмаль в цвет стен (Farrow & Ball No. 241); Ш×Г×В 1800×600×2600 мм | | | изготовление на заказ | шт. | 1 | | пом. 5 |
| М7* | Пенал кухонный, холодильник; корпус ЛДСП, фасады — матовая эмаль в тон стен; Ш×Г×В 600×650×2100 мм | | | изготовление на заказ | шт. | 1 | | пом. 6; крепление к стене |
| М7* | Модуль нижний с мойкой; корпус ЛДСП, фасады — матовая эмаль в тон стен; Ш×Г×В 800×600×900 мм | | | изготовление на заказ | шт. | 1 | | пом. 6 |
| М8* | Модуль нижний: ящики, варочная панель, духовой шкаф, бутылочница; корпус ЛДСП, фасады — матовая эмаль в тон стен; Ш×Г×В 1800×600×900 мм | | | изготовление на заказ | шт. | 1 | | пом. 6 |
| М13 | Навесные шкафы, 3 секции; корпус ЛДСП, фасады — матовая эмаль в тон стен; Ш×Г×В 2200×350×720 мм | | | изготовление на заказ | шт. | 1 | | пом. 6 |
| М14* | Модуль под встраиваемую посудомоечную машину; корпус ЛДСП, фасады — матовая эмаль в тон стен; Ш×Г×В 600×600×900 мм | | | изготовление на заказ | шт. | 1 | | пом. 6 |
| М15* | Вытяжка над варочной панелью; корпус ЛДСП, фасады — матовая эмаль в тон стен; Ш×Г×В 600×400×600 мм | | | изготовление на заказ | шт. | 1 | | пом. 6 |
| | **Мебель покупная** | | | | | | | |
| С1 | Кровать двуспальная; мягкое изголовье, обивка — ткань, цвет Tikkurila H487; Ш×Г×В 1800×2100×450 мм | | | аналог по характеристикам | шт. | 1 | | пом. 1; замена ≤ габарита |
| С2, С3, С8, С9 | Тумба прикроватная; шпон, дуб натуральный, матовое масло; Ш×Г×В 450×400×550 мм | | | аналог по характеристикам | шт. | 4 | | пом. 1, 4; замена ≤ габарита |
| С4 | Стол письменный; шпон, дуб натуральный, матовое масло; Ш×Г×В 1200×600×750 мм | | | аналог по характеристикам | шт. | 1 | | пом. 1; замена ≤ габарита |
| С6 | Кресло; обивка — ткань, цвет Tikkurila H487; Ш×Г×В 800×750×800 мм | | | аналог по характеристикам | шт. | 1 | | пом. 1; замена ≤ габарита |
| С7 | Кровать двуспальная; мягкое изголовье, обивка — ткань, цвет Tikkurila H487; Ш×Г×В 1600×2000×450 мм | | | аналог по характеристикам | шт. | 1 | | пом. 4; замена ≤ габарита |
| С10 | Комод; шпон, дуб натуральный, матовое масло; Ш×Г×В 1200×400×850 мм | | | аналог по характеристикам | шт. | 1 | | пом. 4; крепление к стене; замена ≤ габарита |
| С11 | Кресло для чтения у окна; обивка — ткань, цвет Tikkurila H487; Ш×Г×В 750×750×800 мм | | | аналог по характеристикам | шт. | 1 | | пом. 4; замена ≤ габарита |
| М17 | Банкетка-обувница с мягким сиденьем, над ней настенная вешалка с полкой (низ 1650); шпон, дуб натуральный, матовое масло; Ш×Г×В 800×350×450 мм | | | аналог по характеристикам | шт. | 1 | | пом. 5; замена ≤ габарита |
| М1 | ТВ-тумба с экраном; шпон, дуб натуральный, матовое масло; Ш×Г×В 2000×400×500 мм | | | аналог по характеристикам | шт. | 1 | | пом. 6; замена ≤ габарита |
| М2 | Диван; обивка — ткань, цвет Tikkurila H487; Ш×Г×В 2600×1000×800 мм | | | аналог по характеристикам | шт. | 1 | | пом. 6; замена ≤ габарита |
| М3 | Стол журнальный; шпон, дуб натуральный, матовое масло; Ш×Г×В 1100×550×400 мм | | | аналог по характеристикам | шт. | 1 | | пом. 6; замена ≤ габарита |
| М4 | Кресло; обивка — ткань, цвет Tikkurila H487; Ш×Г×В 800×800×800 мм | | | аналог по характеристикам | шт. | 1 | | пом. 6; замена ≤ габарита |
| М5 | Стол обеденный; шпон, дуб натуральный, матовое масло; Ш×Г×В 1400×900×750 мм | | | аналог по характеристикам | шт. | 1 | | пом. 6; замена ≤ габарита |
| М18 | Стул обеденный к столу М5; обивка — ткань, цвет Tikkurila H487; каркас — дуб натуральный; Ш×Г×В 450×500×820 мм | | | аналог по характеристикам | шт. | 4 | | пом. 6; замена ≤ габарита |
| | **Техника встраиваемая и бытовая, светильники под розетки** | | | | | | | |
| | Стиральная машина, место по листу ВК (П4*); Ш×Г 600×400 мм | | | аналог по характеристикам | шт. | 1 | | пом. 2; по схеме изготовителя |
| | Холодильник встраиваемый, в модуле М6** | | | аналог по характеристикам | шт. | 1 | | пом. 6; по схеме изготовителя |
| | Посудомоечная машина встраиваемая, в модуле М14*; ниша 600 мм | | | аналог по характеристикам | шт. | 1 | | пом. 6; по схеме изготовителя |
| | Варочная панель встраиваемая, электрическая, в модуле М8* | | | аналог по характеристикам | шт. | 1 | | пом. 6; по схеме изготовителя |
| | Духовой шкаф встраиваемый, в модуле М8* | | | аналог по характеристикам | шт. | 1 | | пом. 6; по схеме изготовителя |

## Примечания

1. Позиции мебели совпадают с марками на плане расстановки (лист 26); размеры Ш×Г×В — Ш вдоль стены, Г от стены.
2. Встроенная и корпусная мебель изготавливается по чертежам мебельщика после контрольного обмера; графы «Тип, марка» и «Код продукции» для неё не заполняются (ГОСТ 21.110-2013).
3. Покупные изделия — аналог по характеристикам: заменять только на изделия не больше указанного габарита и того же материала и цвета.
4. Материал и цвет, не указанные в данных изделия, приняты по концепции (лист 25): тон дерева — по полу, обивка — по вторичному цвету палитры; образцы согласовать до заказа.
5. Масса 1 ед. для изделий до 25 кг не указывается. Техника — по монтажным схемам изготовителя; выводы — по листам ЭОМ и ВК.

Допущения и предложения на листе. Знак «*» принято (замерить). Знак «**» предложено (согласовать). См. лист открытых вопросов (листы 6–11).

| Изм. | Кол.уч | Лист | № док. | Подп. | Дата |
|---|---|---|---|---|---|
| Разраб. | | Кырпан А.С. | | | 05.10.26 |
| Пров. | | | | | |
| ГИП | | | | | |
| | | | | | |
| Н. контр. | | | | | |
| Утв. | | | | | |

**ГД-2026-003-АИ**

Трёхкомнатная квартира

Общая площадь 78,95* м² · * размеры со скана, не замерены (реестр — п. 6–11, К-13)

| Дизайн-проект интерьера трёхкомнатной квартиры | Стадия | Лист | Листов |
|---|---|---|---|
| | РП | 27 | 94 |
| **Спецификация мебели и оборудования** М 6/м | **Кырпан Александр Сергеевич** | | |

выпуск 05.10.2026 № 6add39a08d · стр. 31 из 137

# Спецификация мебели и оборудования (продолжение)

Форма 1 ГОСТ 21.110-2013 · позиции мебели — по плану расстановки

ПРЕДВАРИТЕЛЬНО · не для производства работ · открыто пунктов: 31 (реестр — л. 6–11)

| Поз. | Наименование и техническая характеристика | Тип, марка, обозначение документа, опросного листа | Код продукции | Поставщик | Ед. измерения | Кол. | Масса 1 ед., кг | Примечание |
|---|---|---|---|---|---|---|---|---|
| | Вытяжка, в модуле М15** | | | аналог по характеристикам | шт. | 1 | | пом. 6; по схеме изготовителя |
| | Торшер, у поз. С6; абажур — ткань или опаловое стекло; лампа 2700 K | | | аналог по характеристикам | шт. | 1 | | пом. 1; розетка Р5 (ЭОМ) |
| | Торшер, у поз. М1; абажур — ткань или опаловое стекло; лампа 2700 K | | | аналог по характеристикам | шт. | 1 | | пом. 6; розетка Р21 (ЭОМ) |
| | **Текстиль** | | | | | | | |
| Т1 | Портьеры-волна; лён 100 %; цвет Tikkurila H487; карниз 2500 мм, высота 2610 мм, сборка 2 | | | аналог по характеристикам | шт. | 2 | | пом. 1 |
| Т2 | Тюль; полиэстер 100 %; цвет Tikkurila V503; карниз 2500 мм, высота 2610 мм, сборка 2,5 | | | аналог по характеристикам | шт. | 1 | | пом. 1 |
| Т3 | Ковёр под кроватью; шерсть 80 %, хлопок 20 %; цвет NCS S 3005-Y20R; 2800×1850 мм | | | аналог по характеристикам | шт. | 1 | | пом. 1; с подложкой |
| Т4 | Подушки декоративные на кровать; лён 100 %; цвет Tikkurila H487 | | | аналог по характеристикам | шт. | 3 | | пом. 1 |
| Т5 | Подушки на кровать, акцент; хлопковый бархат 100 %; цвет Farrow & Ball No. 30 | | | аналог по характеристикам | шт. | 2 | | пом. 1 |
| Т6 | Плед на кровать; шерсть меринос 100 %; цвет Farrow & Ball No. 30 | | | аналог по характеристикам | шт. | 1 | | пом. 1 |
| Т7 | Портьеры-волна; лён 100 %; цвет Tikkurila H487; карниз 1820 мм, высота 2610 мм, сборка 2 | | | аналог по характеристикам | шт. | 2 | | пом. 4 |
| Т8 | Тюль; полиэстер 100 %; цвет Tikkurila V503; карниз 1820 мм, высота 2610 мм, сборка 2,5 | | | аналог по характеристикам | шт. | 1 | | пом. 4 |
| Т9 | Ковёр под кроватью; шерсть 100 %; цвет Tikkurila V484; 2500×1800 мм | | | аналог по характеристикам | шт. | 1 | | пом. 4; с подложкой |
| Т10 | Подушки декоративные на кровать; букле (шерсть 60 %, полиэстер 40 %); цвет Farrow & Ball No. 229 | | | аналог по характеристикам | шт. | 3 | | пом. 4 |
| Т11 | Подушки на кровать, акцент; хлопковый бархат 100 %; цвет Farrow & Ball No. 47 | | | аналог по характеристикам | шт. | 2 | | пом. 4 |
| Т12 | Плед на кровать; шерсть меринос 100 %; цвет Farrow & Ball No. 30 | | | аналог по характеристикам | шт. | 1 | | пом. 4 |
| Т13 | Портьеры-волна (гостиная); лён 70 %, вискоза 30 %; цвет Tikkurila H487; карниз 2250 мм, высота 2610 мм, сборка 2 | | | аналог по характеристикам | шт. | 2 | | пом. 6 |
| Т14 | Тюль (гостиная); полиэстер 100 %; цвет Tikkurila V503; карниз 2250 мм, высота 2610 мм, сборка 2,5 | | | аналог по характеристикам | шт. | 1 | | пом. 6 |
| Т15 | Римская штора (кухня); лён 100 %; цвет Tikkurila V484; карниз 1400 мм, высота 1620 мм | | | аналог по характеристикам | шт. | 1 | | пом. 6 |
| Т16 | Ковёр в зоне отдыха; шерсть 100 %; цвет Tikkurila V484; 3000×1150 мм | | | аналог по характеристикам | шт. | 1 | | пом. 6; с подложкой |
| Т17 | Подушки на диван; букле (шерсть 60 %, полиэстер 40 %); цвет Tikkurila H487 | | | аналог по характеристикам | шт. | 3 | | пом. 6 |
| Т18 | Подушки на диван, акцент; хлопковый бархат 100 %; цвет Farrow & Ball No. 30 | | | аналог по характеристикам | шт. | 2 | | пом. 6 |
| Т19 | Плед на диван; альпака 50 %, шерсть 50 %; цвет Tikkurila V484 | | | аналог по характеристикам | шт. | 1 | | пом. 6 |
| | **Декор** | | | | | | | |
| ДК1 | Картина над кроватью: абстракция, холст, тонкая рама из дуба; 1200×700 мм; низ на 1300 мм от пола | | | аналог по характеристикам | шт. | 1 | 4 | пом. 1; крепление к стене |
| ДК2 | Зеркало над умывальником, влагостойкое; 600×750 мм; низ на 1100 мм от пола | | | аналог по характеристикам | шт. | 1 | 4 | пом. 2; крепление к стене |
| ДК3 | Картина над кроватью: графика в паспарту, рама — дуб; 1000×700 мм; низ на 1300 мм от пола | | | аналог по характеристикам | шт. | 1 | 4 | пом. 4; крепление к стене |
| ДК4 | Зеркало в рост в тонкой чёрной раме; рама — чёрный матовый; 600×1600 мм; низ на 300 мм от пола | | | аналог по характеристикам | шт. | 1 | 12 | пом. 4; крепление: анкер для пустотелых оснований, 4 шт. |
| ДК5 | Зеркало; рама — чёрный матовый; 600×1800 мм; низ на 550 мм от пола | | | аналог по характеристикам | шт. | 1 | 18 | пом. 5; крепление: анкер, 4 шт. |
| ДК6 | Картина: крупная абстракция в тёплой гамме, холст на подрамнике; 1200×900 мм; центр на 1550 мм от пола | | | аналог по характеристикам | шт. | 1 | 6 | пом. 6; крепление: анкер, 2 шт. |
| ДК7 | Растение в кашпо; 450×450 мм | | | аналог по характеристикам | шт. | 1 | | пом. 6 |
| ДК8 | Ваза керамическая с ветками на обеденном столе; 200×350 мм; на М5 | | | аналог по характеристикам | шт. | 1 | | пом. 6 |
| ДК9 | Зеркало над умывальником, влагостойкое; 500×700 мм; низ на 1100 мм от пола | | | аналог по характеристикам | шт. | 1 | 4 | пом. 7; крепление к стене |

**Допущения и предложения на листе**

Основа листа: размеры сняты со скана плана заказчика по размерным цепочкам, контрольный обмер на объекте не выполнялся (К-13); высота потолка 2700 мм принята: на плане заказчика не указана (К-11); толщины стен приняты: наружные 250 мм, перегородки 150 мм (на плане 85–190 мм) (К-13); разрешённая мощность 15 кВт принята по типовой квартире, технических условий нет (К-14); утолщение стены 190 × 1360 мм и элемент 1470 × 160 мм плана заказчика не определены (К-12); ниши санузла 2 закрыты перегородкой и фальш-стеной: проектное решение, на плане заказчика ниша у входа открыта (К-18); несущие стены не определены: до технического заключения все существующие стены считаются несущими (К-20); окна существующие и сохраняются; подоконная доска и глубина откосов не заданы — приняты, не замерены (К-27).

Знак «**» — предложение проектировщика, заказчиком не утверждено (согласовать с заказчиком): ИЗ-5, К-8: М15.

См. лист открытых вопросов (лист 6, записи К-8, К-11; лист 7, записи К-12–К-14, К-18, К-20; лист 8, запись К-27; лист 9, запись ИЗ-5).

| Изм. | Кол.уч | Лист | № док. | Подп. | Дата |
|---|---|---|---|---|---|
| Разраб. | | Кырпан А.С. | | | 05.10.26 |
| Пров. | | | | | |
| ГИП | | | | | |
| | | | | | |
| Н. контр. | | | | | |
| Утв. | | | | | |

**ГД-2026-003-АИ**

Трёхкомнатная квартира

Общая площадь 78,95* м² · * размеры со скана, не замерены (реестр — п. 6–11, К-13)

| Дизайн-проект интерьера трёхкомнатной квартиры | Стадия | Лист | Листов |
|---|---|---|---|
| | РП | 28 | 94 |
| **Спецификация мебели и оборудования (продолжение)** М 6/м | **Кырпан Александр Сергеевич** | | |

выпуск 05.10.2026 · 6add39ab8d · стр. 32 из 137

03

# Электрооборудование

Кырлан Александр Сергеевич

выпуск 05.10.2026 № 6add39ab8d · стр. 33 из 137

# План розеток и электровыводов

Розетки, выводы кабеля, щит · размеры в мм · высоты от чистого пола

ПРЕДВАРИТЕЛЬНО · не для производства работ · открыто пунктов: 31 (реестр — л. 6–11)

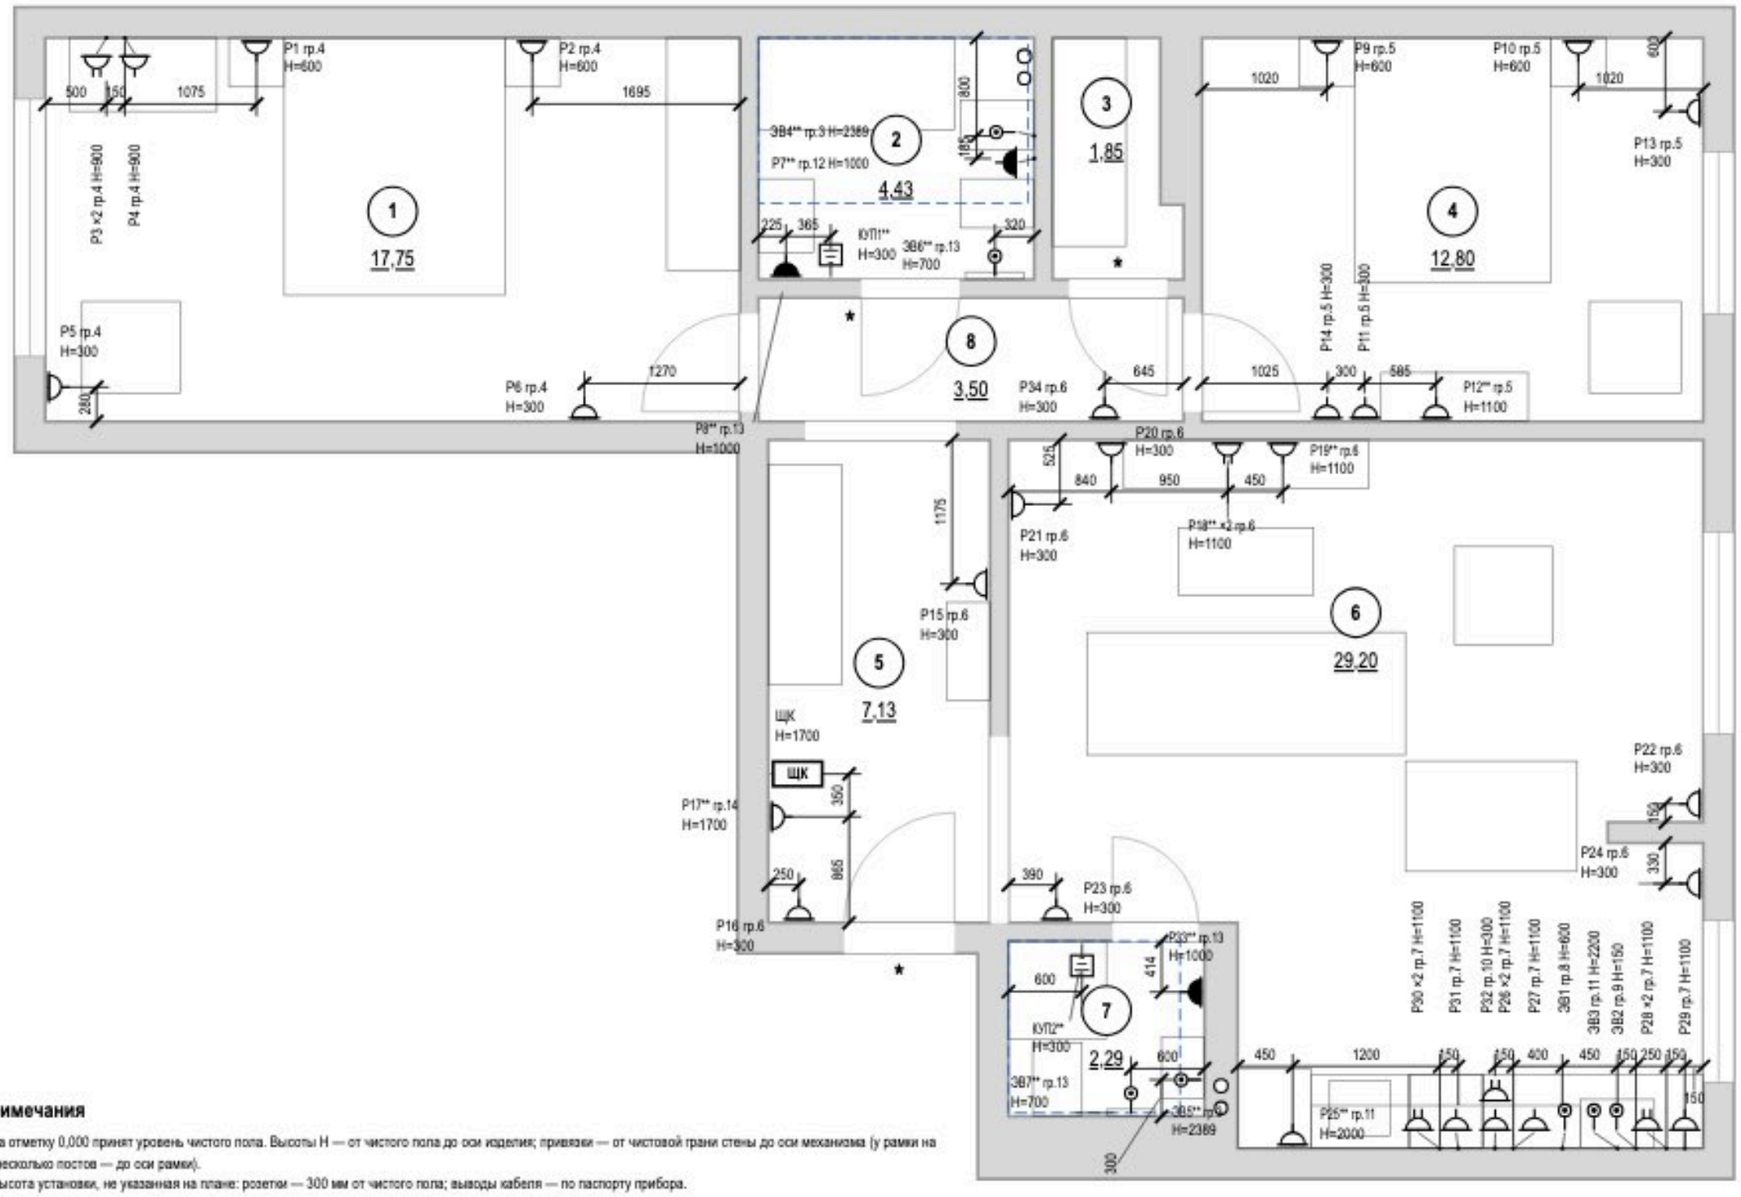


## Условные обозначения

- розетка с заземляющим контактом; у знака — марка, ×N постов в рамке, гр. — группа щита, H — высота оси, мм
- то же, рамка на 2 поста (число черточек — число постов)
- розетка влагозащищённая IP44
- вывод кабеля для подключения прибора (без розетки), марка ЭВ
- КУП — коробка уравнивания потенциалов (ДСУП), проводник к шине PE щита
- ЩК — щит квартирный
- знак разведён для читаемости: точка на стене — у выносок, привязка — до неё
- граница зоны 2 ванной (600 мм от ванны/поддона)
- мебель и сантехприборы — подложка
- стояк: К1 — канализация, В1 — ХВС, Т3 — ГВС
- 1 — номер помещения, площадь м²

Допущения и предложения на листе. Основа листа: размеры сняты со скана плана заказчика по размерным цепочкам, контрольный обмер на объекте не выполнялся (К-13); высота потолка 2700 мм принята: на плане заказчика не указана (К-11); толщины стен приняты: наружные 250 мм, перегородки 150 мм (на плане 85–190 мм) (К-13); разрешённая мощность 15 кВт принята по типовой квартире, технических условий нет (К-14); утолщение стены 190 × 1360 мм и элемент 1470 × 160 мм плана заказчика не определены (К-12); ниши санузла 2 закрыты перегородкой и фальш-стеной: проектное решение, на плане заказчика ниша у входа открыта (К-18); несущие стены не определены: до технического заключения все существующие стены считаются несущими (К-20); окна существующие и сохраняются; подоконная доска и глубина откосов не заданы — приняты, не замерены (К-27). Знак «*» — принято, не замерено и не подтверждено (замерить на объекте): ИЗ-11, К-19: П4 — вертикальная загрузка 400 × 600 мм — условие закупки (решение автора, ИЗ-11); модель не выбрана, габарит сверить по паспорту; К-17: Ст К1-1, Ст В1-1, Ст К1-2, Ст В1-2. Знак «**» — предложение проектировщика, заказчиком не утверждено (согласовать с заказчиком): ИЗ-8: ЭВ4, ЭВ6 — вывод к бытовому вентилятору, таймер выбега; КУП1, КУП2 — коробка уравнивания потенциалов, проводник от шины PE; К-7: Р12 — высота 1100 мм выше нормы 1 м (ПУЭ 6.6.30) по назначению: питание ТВ над комодом, в одной зоне с выводами ТВ2 и LAN2; Р17 — высота 1700 мм выше нормы 1 м (ПУЭ 6.6.30) по назначению: питание слаботочного щита ЩС, рядом со щитом на его высоте; Р18 — высота 1100 мм выше нормы 1 м (ПУЭ 6.6.30) по назначению: питание ТВ, в одной зоне с выводами ТВ1 и LAN3; Р19 — высота 1100 мм выше нормы 1 м (ПУЭ 6.6.30) по назначению: питание приставки ТВ, в одной зоне с выводами ТВ1 и LAN3; К-7, К-8: Р25 — высота 2000 мм выше нормы 1 м (ПУЭ 6.6.30) по назначению: питание встроенного холодильника М6, розетка над нишей за съёмной панелью. См. лист открытых вопросов (лист 6, записи К-1, К-7, К-8, К-11; лист 7, записи К-12–К-14, К-17–К-20; лист 8, записи К-25–К-27; лист 9, записи ИЗ-1, ИЗ-4, ИЗ-5, ИЗ-8, ИЗ-9; лист 10, записи ИЗ-11, ИЗ-15); по листу — К-1, К-7, К-8, ИЗ-15.

## Примечания

1. За отметку 0,000 принят уровень чистого пола. Высоты H — от чистого пола до оси изделия; привязки — от чистовой грани стены до оси механизма (у рамки на несколько постов — до оси рамки).
2. Высота установки, не указанная на плане: розетки — 300 мм от чистого пола; выводы кабеля — по паспорту прибора.
3. Розетки в санузле — только вне зон 0–2 (ПУЭ 7.1.48, ГОСТ Р 50571.7.701-2024), IP44, через УЗО 30 мА.
4. Розеточные и мокрые линии — через УЗО или дифавтомат с током утечки не более 30 мА (ПУЭ 7.1.79); в санузле выполнить ДСУП (ПУЭ 7.1.87–7.1.88).
5. Кабель — медный, исполнение нг(A)-LS (ГОСТ 31565-2012); скрытая прокладка только горизонтально и вертикально, фактические трассы зафиксировать исполнительной схемой до закрытия отделкой.
6. Расчёт нагрузок, токов КЗ, селективности и сечений — по проекту ЭОМ организации с допуском СРО; лист задаёт состав, расположение и группы.
7. Выводы кухонной техники — после утверждения проекта кухни (ориентировочно); привязки выводов даны от осей модулей гарнитура и пересматриваются вместе с проектом кухни.
8. Допущение проекта: кухня: раскладка гарнитура принята проектной, решение автора (ИЗ-12) — мойка М7* у шахты Ш2, ПММ М14* рядом с мойкой, варочная и духовой шкаф в М8*, вытяжка М15**, холодильник М6**; выводы техники — по типовой расстановке; условие: до начала черновых работ сверить раскладку и выводы с чертежом кухни от изготовителя, выводы пересматриваются по его чертежу (вопрос К-8).
9. Допущение проекта: стиральная машина П4* — вертикальной загрузки, габарит в плане 400 × 600 мм (ширина 400 вдоль стены Б): условие закупки, а не пожелание, решение автора (ИЗ-11); машина с фронтальной загрузкой или большего габарита не подходит — перед люком ванна П1; модель не выбрана, габарит и подводку сверить по паспорту до закрытия трасс (вопрос К-19).
10. Марки из допущений, которых нет на этом листе: М7*, М14*, М15** — лист 59; Ш2 — лист 39; П1, П4* — лист 39.
11. Электрический тёплый пол проектом не предусмотрен; при решении заказчика устроить — отдельный лист «План тёплых полов»: контуры с отступом 100 мм от стен и мебели без ножек, датчик в гофре, терморегулятор, своя группа щита через УЗО 30 мА.
12. Ведомости электроточек, изделий, светильников и расшифровка клавиш — лист 32.

1000 мм · печать 1:1

| Изм. | Кол.уч | Лист | № док. | Подп. | Дата |
|---|---|---|---|---|---|
| Разраб. | | Кырпан А.С. | | | 05.10.26 |
| Пров. | | | | | |
| ГИП | | | | | |
| Н. контр. | | | | | |
| Утв. | | | | | |

**ГД-2026-003-АИ**

Трёхкомнатная квартира

Общая площадь 78,95* м² · * размеры со скана, не замерены (реестр — п. 6–11, К-13)

Дизайн-проект интерьера трёхкомнатной квартиры

| Стадия | Лист | Листов |
|---|---|---|
| РП | 29 | 94 |

**План розеток и электровыводов**

М 1:50

Кырпан Александр Сергеевич

выпуск 05.10.2026 · 6add39ab8d · стр. 34 из 137

# План освещения

Светильники, группы включения, извещатели · размеры в мм

ПРЕДВАРИТЕЛЬНО · не для производства работ · открыто пунктов: 31 (реестр — л. 6–11)

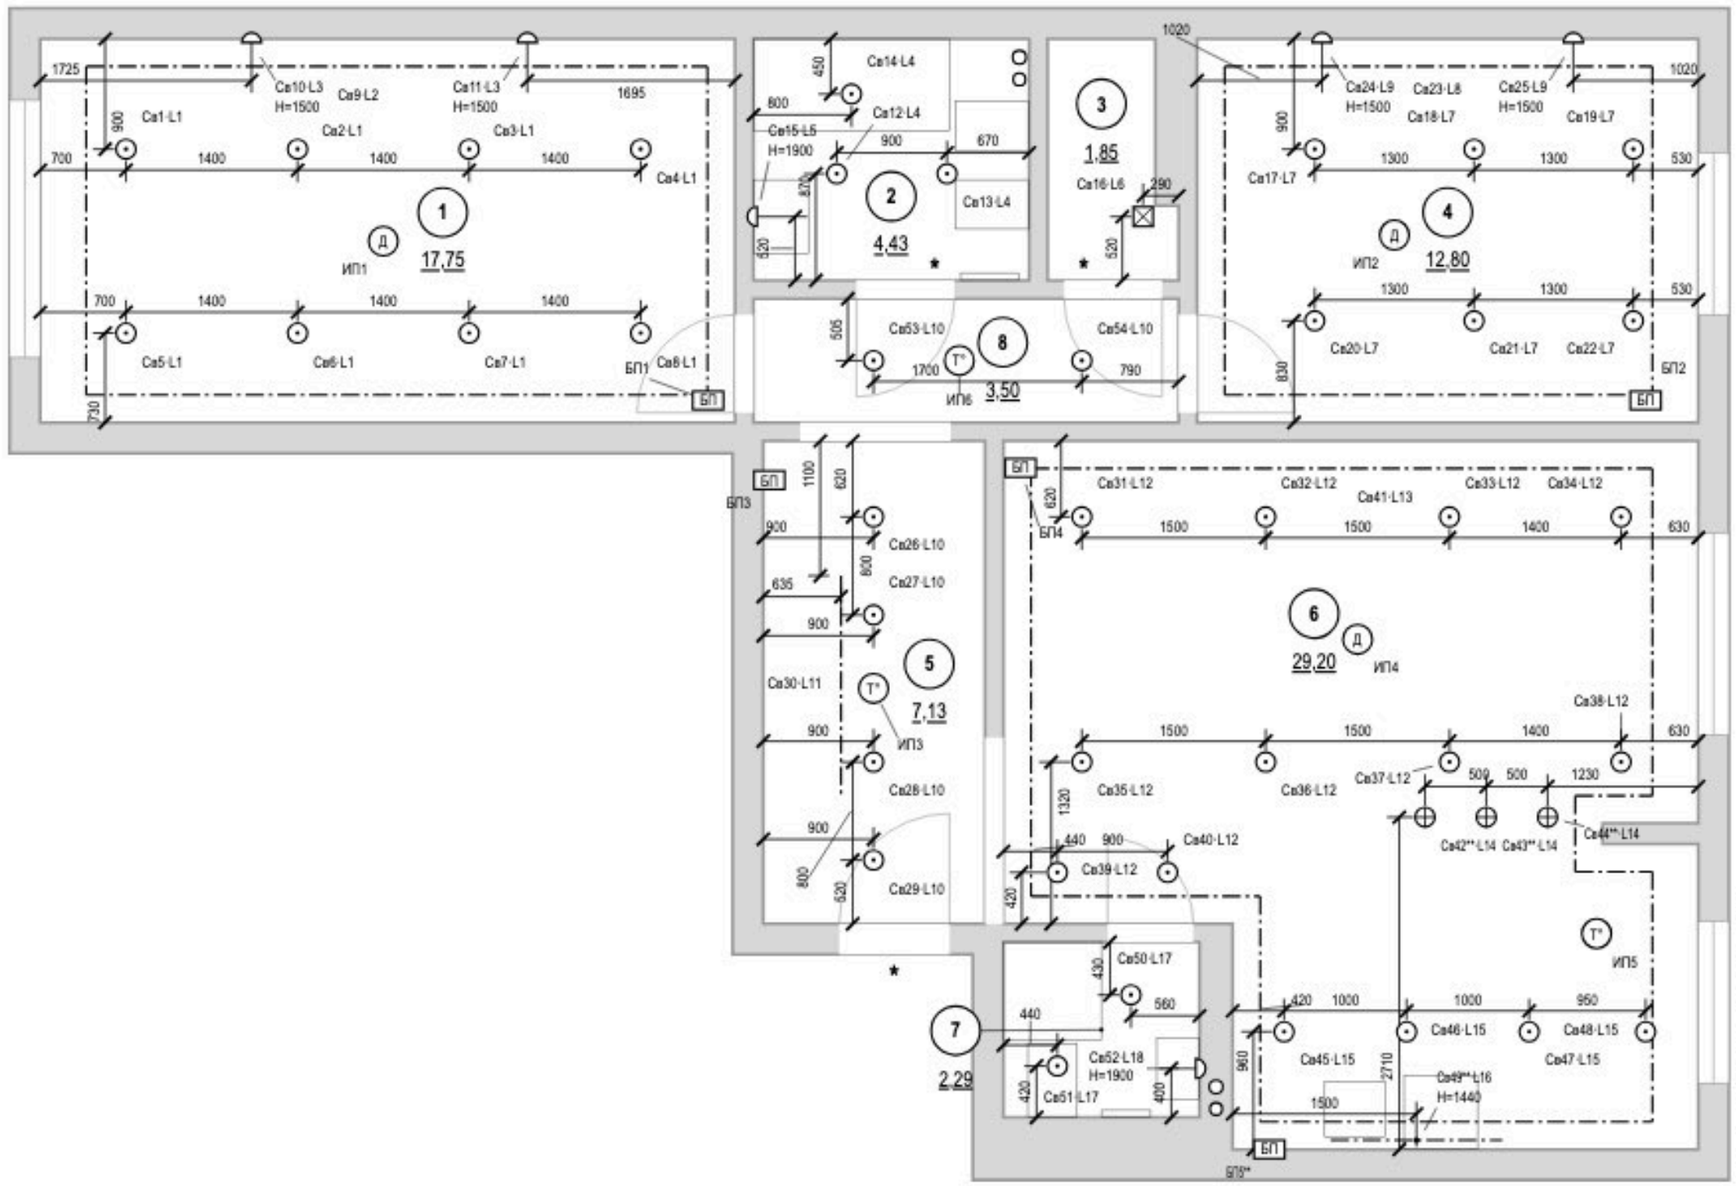


## Условные обозначения

- светильник встраиваемый точечный
- светильник потолочный накладной
- светильник подвесной
- светильник настенный (бра), H — высота оси
- линейный светильник настенный (подсветка столешницы), точка — вывод питания
- светодиодная лента в профиле / в карнизе короба
- Св1·L1 — марка светильника (как в ведомости и на развёртках) · группа включения L (лист выключателей)
- Д — извещатель пожарный дымовой автономный
- T° — извещатель пожарный тепловой
- БП — блок питания LED, с доступом (люк от 100×100 мм)
- 1 — номер помещения, площадь м²

## Освещённость (оценка)

| Пом. | S, м² | Ен, лк | Φ треб., лм | Φ по пр., лм |
|---|---|---|---|---|
| 1 | 17,8 | 150 | 7500 | 8000 |
| 2 | 4,4 | 50 | 620 | 1500 |
| 3 | 1,9 | 75 | 390 | 900 |
| 4 | 12,8 | 150 | 5410 | 6300 |
| 5 | 7,1 | 50 | 1000 | 2400 |
| 6 | 29,2 | 150 | 12340 | 16000 |
| 7 | 2,3 | 50 | 320 | 1100 |
| 8 | 3,5 | 50 | 490 | 1200 |

Допущения и предложения на листе. Основа листа: размеры сняты со скана плана заказчика по размерным цепочкам, контрольный обмер на объекте не выполнялся (К-13); высота потолка 2700 мм принята: на плане заказчика не указана (К-11); толщины стен приняты: наружные 250 мм, перегородки 150 мм (на плане 85–190 мм) (К-13); разрешённая мощность 15 кВт принята по типовой квартире, технических условий нет (К-14); утолщение стены 190 × 1360 мм и элемент 1470 × 160 мм плана заказчика не определены (К-12); ниши санузла 2 закрыты перегородкой и фальш-стеной: проектное решение, на плане заказчика ниша у входа открыта (К-18); несущие стены не определены: до технического заключения все существующие стены считаются несущими (К-20); окна существующие и сохраняются; подоконная доска и глубина откосов не заданы — приняты, не замерены (К-27). Знак «*» — принято, не замерено и не подтверждено (замерить на объекте): К-17: Ст К1-1, Ст В1-1, Ст К1-2, Ст В1-2. Знак «**» — предложение проектировщика, заказчиком не утверждено (согласовать с заказчиком): ИЗ-3: Св42, Св43, Св44, Св49, БП5 — диммируемость добавлена разработчиком проекта под светорегуляторы S11 и S12. См. лист открытых вопросов (лист 6, запись К-11; лист 7, записи К-12–К-14, К-17, К-18, К-20; лист 8, записи К-25–К-27; лист 9, запись ИЗ-3).

## Примечания

1. За отметку 0,000 принят уровень чистого пола. Высоты H — от чистого пола до оси изделия; привязки — от чистовой грани стены до оси механизма (у рамки на несколько постов — до оси рамки).
2. Высота установки, не указанная на плане: светильники — на потолке; настенные — по отметке H у знака. Привязки — до оси светильника от чистовой грани стены, по рядам.
3. Освещённость: Ен — СанПиН 1.2.3685-21, табл. 5.52 (на полу); Φ треб. = Ен·S/(U·MF) при U = 0,5 и MF = 0,71 (СП 52.13330.2016, табл. 4.3) — оценка, не светотехнический расчёт. Декоративная подсветка в Φ не входит.
4. Во влажных помещениях — светильники не ниже IP44; в зонах 0–2 ванной — по ГОСТ Р 50571.7.701-2024 (зона 1 — IPX5).
5. LED-лента в карнизе подсветки короба — по линии карниза с плана потолков; блок питания — в люке короба (БП на плане), питание ленты длиннее 5 м — с двух концов.
6. Розеточные и мокрые линии — через УЗО или дифавтомат с током утечки не более 30 мА (ПУЭ 7.1.79); в санузле выполнить ДСУП (ПУЭ 7.1.87–7.1.88).
7. Кабель — медный, исполнение нг(A)-LS (ГОСТ 31565-2012); скрытая прокладка только горизонтально и вертикально, фактические трассы зафиксировать исполнительной схемой до закрытия отделкой.
8. Расчёт нагрузок, токов КЗ, селективности и сечений — по проекту ЭОМ организации с допуском СРО; лист задаёт состав, расположение и группы.
9. Ведомость светильников — лист 32.

1000 мм · печать 1:1

| Изм. | Кол.уч | Лист | № док. | Подп. | Дата |
|---|---|---|---|---|---|
| Разраб. | | Кырпан А.С. | | | 05.10.26 |
| Пров. | | | | | |
| ГИП | | | | | |
| | | | | | |
| Н. контр. | | | | | |
| Утв. | | | | | |

**ГД-2026-003-АИ**

Трёхкомнатная квартира

Общая площадь 78,95* м² · * размеры со скана, не замерены (реестр — л. 6–11, К-13)

Дизайн-проект интерьера трёхкомнатной квартиры

| Стадия | Лист | Листов |
|---|---|---|
| РП | 30 | 94 |

**План освещения**

М 1:50

Кырпан Александр Сергеевич

выпуск 05.10.2026 № 6add39ab8d · стр. 35 из 137

# План выключателей и схема включения

Выключатели S, группы включения L, линии связи · размеры в мм

ПРЕДВАРИТЕЛЬНО · не для производства работ · открыто пунктов: 31 (реестр — л. 6–11)

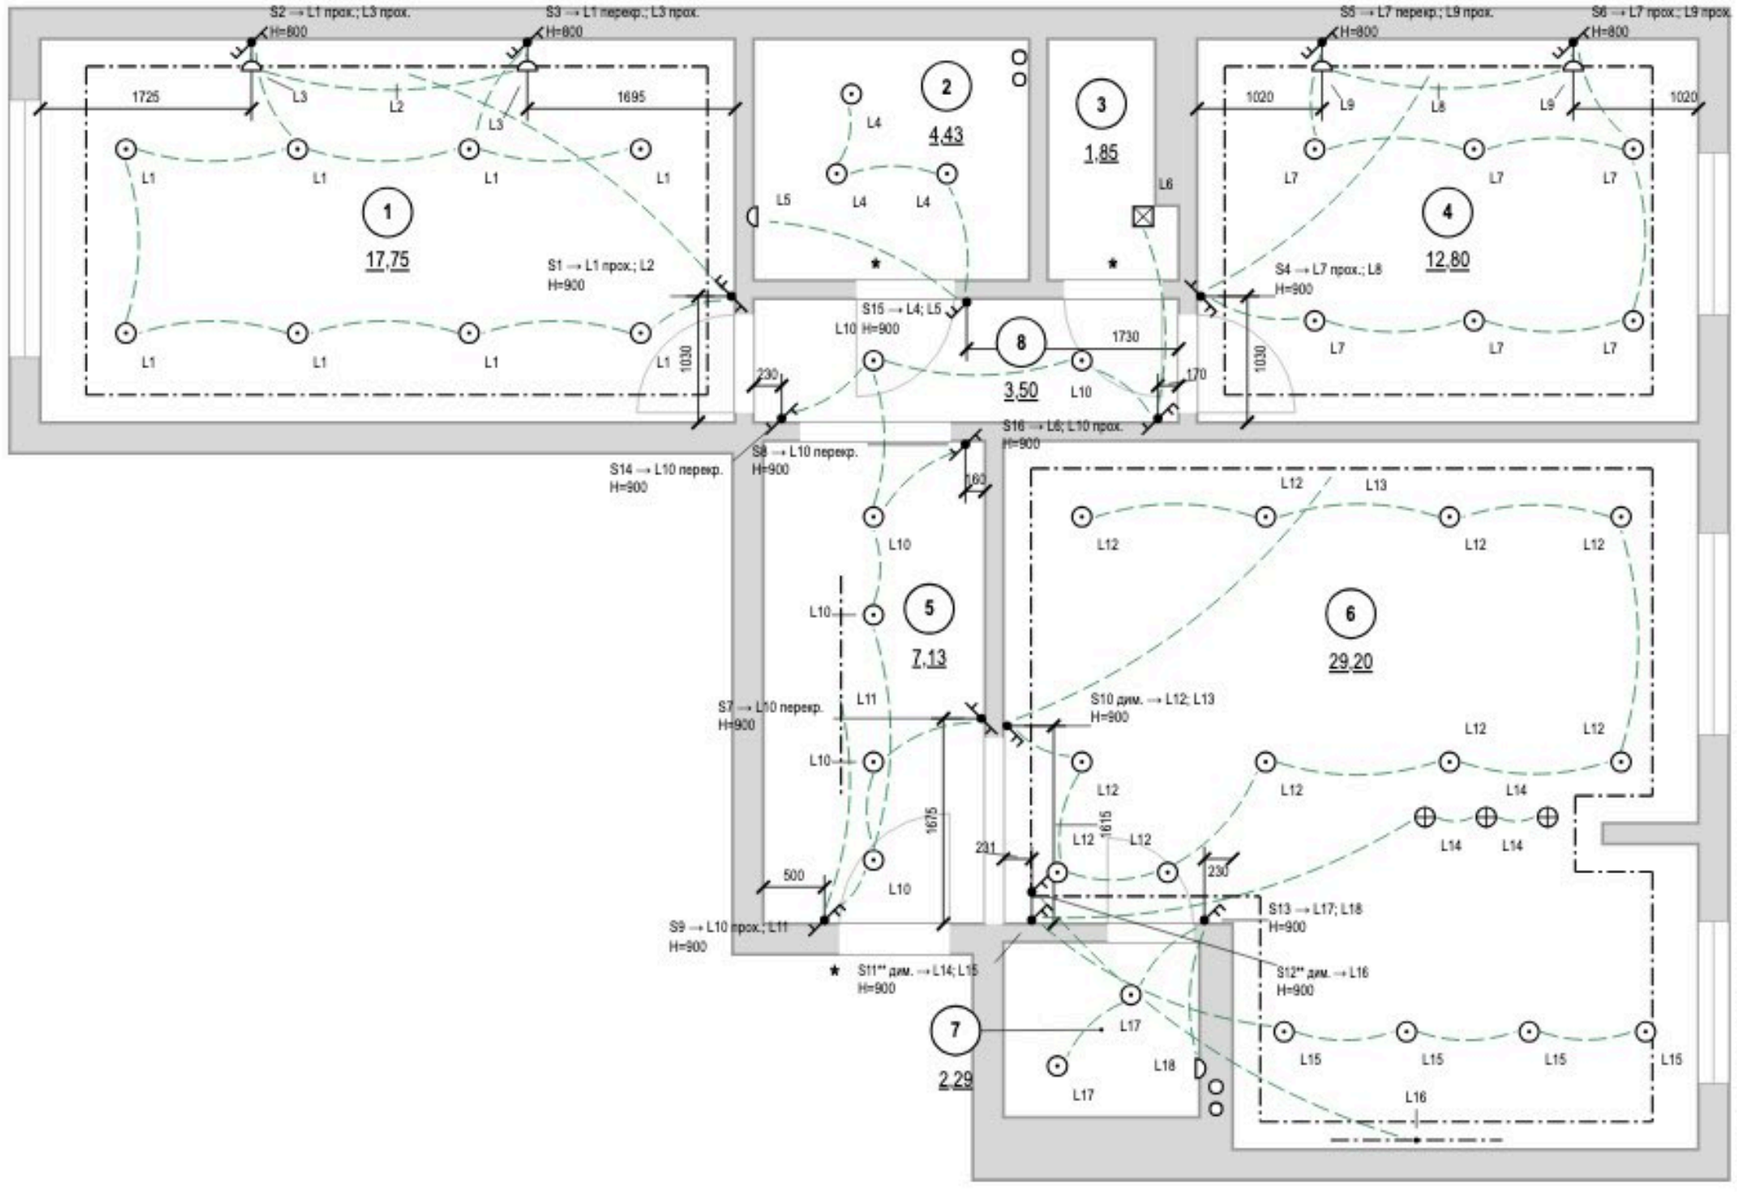


## Условные обозначения

- выключатель одноклавишный
- выключатель двухклавишный (флажков — по числу клавиш)
- выключатель с проходной или перекрёстной клавишей (обратный флажок); тип клавиши — в подписи
- S1 → — марка → группы по клавишам (через «;»): прох. — проходной, перекр. — перекрёстный, дим. — светорегулятор; H — высота
- линия связи: выключатель → светильники группы (не трасса кабеля)
- светильник встраиваемый точечный
- светильник потолочный накладной
- светильник подвесной
- светильник настенный (бра), H — высота оси
- линейный светильник настенный (подсветка столешницы), точка — вывод питания
- светодиодная лента в профиле / в карнизе короба
- L1 — группа включения у светильника
- (1) — номер помещения, площадь м²

**Допущения и предложения на листе**

Основа листа: размеры сняты со скана плана заказчика по размерным цепочкам, контрольный обмер на объекте не выполнялся (К-13); высота потолка 2700 мм принята: на плане заказчика не указана (К-11); толщины стен приняты: наружные 250 мм, перегородки 150 мм (на плане 85–190 мм) (К-13); разрешённая мощность 15 кВт принята по типовой квартире, технических условий нет (К-14); утолщение стены 190 × 1360 мм и элемент 1470 × 160 мм плана заказчика не определены (К-12); ниши санузла 2 закрыты перегородкой и фальш-стенкой: проектное решение, на плане заказчика ниша у входа открыта (К-18); несущие стены не определены: до технического заключения все существующие стены считаются несущими (К-20); окна существующие и сохраняются; подоконная доска и глубина откосов не заданы — приняты, не замерены (К-27).

Знак «*» — принято, не замерено и не подтверждено (замерить на объекте): К-17: Ст К1-1, Ст В1-1, Ст К1-2, Ст В1-2; К-25: дверь пом. 8 (стена А) — толщина стены в проёме принята 150 мм (как у всех перегородок модели), по скану плана заказчика стена 85 мм — не замерено (К-25); проём существующий, скрытый блок ставится в него с зазором 10–15 мм на сторону, полотно уже проёма; узел скрытой двери выполнен для принятой толщины 150 мм; К-26: дверь пом. 5 (стена В) — входная дверь существующая; по плану заказчика полотно открывается наружу, в общий коридор — направление взято с плана и на объекте не проверено; остаётся ли существующий блок или он заменяется — не решено (К-26).

Знак «**» — предложение проектировщика, заказчиком не утверждено (согласовать с заказчиком): ИЗ-3: S11, S12 — светорегулятор добавлен разработчиком проекта.

См. лист открытых вопросов (лист 6, запись К-11; лист 7, записи К-12–К-14, К-17, К-18, К-20; лист 8, записи К-25–К-27; лист 9, запись ИЗ-3).

## Примечания

1. За отметку 0,000 принят уровень чистого пола. Высоты H — от чистого пола до оси изделия; привязки — от чистовой грани стены до оси механизма (у рамки на несколько постов — до оси рамки).
2. Высота установки, не указанная на плане: выключатели — 900 мм от чистого пола, со стороны дверной ручки (ПУЭ 7.1.51).
3. Линии связи показывают, какой выключатель какую группу L включает; это не трасса кабеля. Трасса — принципиальная, фактическую зафиксировать исполнительной схемой.
4. Группы из нескольких мест (L1 — S1, S2, S3; L3 — S2, S3; L7 — S4, S5, S6; L9 — S5, S6; L10 — S7, S8, S9, S14, S16): на крайних местах — проходные клавиши, на промежуточных — перекрёстные; механизмы — в ведомости изделий.
5. Светорегулятор — по заднему фронту (для LED-драйверов), совместимость с драйверами проверить до закупки.
6. Розеточные и мокрые линии — через УЗО или дифавтомат с током утечки не более 30 мА (ПУЭ 7.1.79); в санузле выполнить ДСУП (ПУЭ 7.1.87–7.1.88).
7. Кабель — медный, исполнение нг(A)-LS (ГОСТ 31565-2012); скрытая прокладка только горизонтально и вертикально, фактические трассы зафиксировать исполнительной схемой до закрытия отделкой.
8. Расчёт нагрузок, токов КЗ, селективности и сечений — по проекту ЭОМ организации с допуском СРО; лист задаёт состав, расположение и группы.
9. Расшифровка клавиш и ведомость изделий — лист 32.

1000 мм · печать 1:1

| | | | | | | | |
|---|---|---|---|---|---|---|---|
| | | | | | | ГД-2026-003-АИ | |
| | | | | | | Трёхкомнатная квартира | |
| | | | | | | Общая площадь 78,95* м² · * размеры со скана, не замерены (реестр — л. 6–11, К-13) | |
| Изм. | Кол.уч | Лист | № док. | Подп. | Дата | Дизайн-проект интерьера трёхкомнатной квартиры | Стадия: РП; Лист: 31; Листов: 94 |
| Разраб. | | Кырпан А.С. | | | 05.10.26 | План выключателей и схема включения | Кырпан Александр Сергеевич |
| Пров. | | | | | | М 1:50 | |
| ГИП | | | | | | | |
| Н. контр. | | | | | | | |
| Утв. | | | | | | | |

выпуск 05.10.2026 · 6add39ab8d · стр. 36 из 137

# Ведомость электроточек и изделий

Электроточки, изделия, светильники, клавиши выключателей · 6/м

## Ведомость электроточек

| Марка | Пом. | Назначение | Н, мм | Гр. |
|---|---|---|---|---|
| Р1 | 1 | у кровати | 600 | 4 |
| Р2 | 1 | у кровати | 600 | 4 |
| Р3 | 1 | рабочий стол | 900 | 4 |
| Р4 | 1 | рабочий стол | 900 | 4 |
| Р5 | 1 | торшер у кресла | 300 | 4 |
| Р6 | 1 | уборка | 300 | 4 |
| КУП1** | 2 | КУП — уравнивание потенциалов (ДСУП) | 300 | |
| Р7** | 2 | стиральная машина, IP44 | 1000 | 12 |
| Р8* | 2 | фен у умывальника, IP44 | 1000 | 13 |
| ЗВ4** | 2 | вентилятор ВР1 (таймер выбега) | 2389 | 3 |
| ЗВ6** | 2 | полотенцесушитель П10**, IP44 | 700 | 13 |
| Р9 | 4 | у кровати | 600 | 5 |
| Р10 | 4 | у кровати | 600 | 5 |
| Р11 | 4 | у комода | 300 | 5 |
| Р12** | 4 | ТВ над комодом (в одной зоне с ТВ2, LAN2) | 1100 | 5 |
| Р13 | 4 | уборка | 300 | 5 |
| Р14 | 4 | уборка у входа | 300 | 5 |
| Р15 | 5 | пылесос, сушилка обуви | 300 | 6 |
| Р16 | 5 | уборка | 300 | 6 |
| Р17** | 5 | питание слаботочного щита (рядом с ЩС**) | 1700 | 14 |
| ЩК | 5 | щит квартирный ЩРВ-П-48 | 1700 | |
| Р18** | 6 | ТВ (в одной зоне с ТВ1, LAN3) | 1100 | 6 |
| Р19** | 6 | ТВ-приставка (в одной зоне с ТВ1, LAN3) | 1100 | 6 |
| Р20 | 6 | у ТВ-тумбы | 300 | 6 |
| Р21 | 6 | торшер | 300 | 6 |
| Р22 | 6 | у кресла | 300 | 6 |
| Р23 | 6 | уборка, пылесос | 300 | 6 |
| Р24 | 6 | у обеденного стола | 300 | 6 |

## Ведомость электроточек (продолжение)

| Марка | Пом. | Назначение | Н, мм | Гр. |
|---|---|---|---|---|
| Р25** | 6 | холодильник, над нишей М6** (съёмная панель) | 2000 | 11 |
| Р26 | 6 | фартук | 1100 | 7 |
| Р27 | 6 | фартук | 1100 | 7 |
| Р28 | 6 | фартук | 1100 | 7 |
| Р29 | 6 | фартук | 1100 | 7 |
| Р30 | 6 | фартук между мойкой и варочной | 1100 | 7 |
| Р31 | 6 | фартук между мойкой и варочной | 1100 | 7 |
| Р32 | 6 | посудомоечная машина | 300 | 10 |
| ЗВ1 | 6 | варочная панель (в соседнем модуле М8*.3, за ящиком) | 600 | 8 |
| ЗВ2 | 6 | духовой шкаф | 150 | 9 |
| ЗВ3 | 6 | вытяжка | 2200 | 11 |
| КУП2** | 7 | КУП — уравнивание потенциалов (ДСУП) | 300 | |
| Р37* | 7 | фен у умывальника, IP44 | 1000 | 13 |
| ЗВ5** | 7 | вентилятор ВР3 (таймер выбега) | 2389 | 3 |
| ЗВ7** | 7 | полотенцесушитель П13**, IP44 | 700 | 13 |
| Р34 | 8 | уборка | 300 | 6 |

## Ведомость изделий

| Наименование | Марки | Ед. | Кол. |
|---|---|---|---|
| Розетка с з/к и защитными шторками, 16 А | по ведомости точек | шт | 36 |
| Розетка IP44 с крышкой, 16 А | Р7**, Р8**, Р37* | шт | 3 |
| Выключатель 1-клав. перекрёстный | S7, S8, S14 | шт | 3 |
| Выключатель 2-клав. | S13, S15 | шт | 2 |
| Выключатель 2-клав. (перекрёстная + проходная) | S3, S5 | шт | 2 |
| Выключатель 2-клав. (проходная + обычная) | S1, S4, S9, S16 | шт | 4 |
| Выключатель 2-клав. проходной | S2, S6 | шт | 2 |
| Светорегулятор 1-канальный, задний фронт (LED) | S12** | шт | 1 |

## Ведомость изделий (продолжение)

| Наименование | Марки | Ед. | Кол. |
|---|---|---|---|
| Светорегулятор 2-канальный, задний фронт (LED) | S10, S11** | шт | 2 |
| Датчик движения ночной подсветки | L11 | шт | 1 |
| Рамка 1-постовая | в т. ч. 16 под выключ. | шт | 45 |
| Рамка 2-постовая | | шт | 5 |
| Коробка установочная (подрозетник) Ø68 | розетки, выключатели | шт | 55 |
| Вывод кабеля под прибор (клеммник) | ЗВ1–ЗВ3, ЗВ4**, ЗВ6**, ЗВ8**, ЗВ7** | шт | 7 |
| Коробка уравнивания потенциалов КУП | КУП1**, КУП2** | шт | 2 |
| Блок питания LED 24 В, 200 Вт, дим. | БП1, БП2 | шт | 2 |
| Блок питания LED 24 В, 20 Вт | БП3 | шт | 1 |
| Блок питания LED 24 В, 300 Вт, дим. | БП4 | шт | 1 |
| Блок питания LED 24 В, 60 Вт, дим. | БП5** | шт | 1 |
| Извещатель дымовой автономный | ИП1, ИП2, ИП4 | шт | 3 |
| Извещатель тепловой | ИП3, ИП5, ИП6 | шт | 3 |
| Щит квартирный (состав — лист щита) | ЩК | шт | 1 |
| Розетка компьютерная RJ45, кат. 6, с рамкой и подрозетником | LAN1–LAN3 | шт | 3 |
| Розетка телевизионная (коаксиальная) с рамкой и подрозетником | ТВ1, ТВ2 | шт | 2 |
| Точка доступа Wi-Fi (оборудование заказчика), питание PoE | AP1**, AP2** | шт | 2 |
| Трубка или монитор домофона (поставка домофонной организации) | ДФ1 | шт | 1 |
| Щит слаботочный ЩС**: корпус, DIN-рейка, розетки 220 В | ЩС** | шт | 1 |
| Патч-панель, портов не менее 5 | | шт | 1 |
| Коммутатор, портов не менее 5, из них PoE 2 | | шт | 1 |

## Ведомость изделий (продолжение)

| Наименование | Марки | Ед. | Кол. |
|---|---|---|---|
| Кабель домофона — тип по системе поставщика (по лучам от ЩС**, запас 10 %) | | м | 2,9 |
| Кабель коаксиальный RG-6 (75 Ом) к розеткам ТВ (по лучам от ЩС**, запас 10 %) | | м | 29,1 |
| Кабель U/UTP кат. 6 (LAN, Wi-Fi и камеры по PoE) (по лучам от ЩС**, запас 10 %) | | м | 61,2 |

## Ведомость светильников

| Поз. | Марки | Тип | Кол. | P, Вт | Ф, лм | IP | Tц/Ra |
|---|---|---|---|---|---|---|---|
| 1 | Св1–Св8 | встраиваемый точечный | 8 | 12 | 1000 | | 270090 |
| 2 | Св9 | светодиодная лента, 15,5 м | 1 | 148,8 | 13950 | | 270090 |
| 3 | Св10, Св11, Св24, Св25 | настенный (бра), H=1500 | 4 | 6 | 400 | | 270090 |
| 4 | Св12–Св14, Св51 | встраиваемый точечный | 4 | 6 | 500 | 44 | 300090 |
| 5 | Св15, Св52 | настенный (бра), H=1900 | 2 | 8 | 600 | 44 | 300090 |
| 6 | Св16 | потолочный накладной | 1 | 10 | 900 | | 300090 |
| 7 | Св17–Св22 | встраиваемый точечный | 6 | 12 | 1050 | | 270090 |
| 8 | Св23 | светодиодная лента, 12,3 м | 1 | 118,1 | 11070 | | 270090 |
| 9 | Св26–Св29, Св53, Св54 | встраиваемый точечный | 6 | 7 | 600 | | 300090 |
| 10 | Св30 | светодиодная лента, 1,8 м | 1 | 8,6 | 270 | | 270090 |
| 11 | Св31–Св40 | встраиваемый точечный | 10 | 12 | 1000 | | 300090 |
| 12 | Св41 | светодиодная лента, 22,1 м | 1 | 212,2 | 19890 | | 270090 |
| 13 | Св42**, Св43**, Св44** | подвесной | 3 | 9 | 800 | | 300090 |
| 14 | Св45–Св48 | встраиваемый точечный | 4 | 10 | 900 | | 300090 |
| 15 | Св49** | линейный светильник, H=1440 | 1 | 18 | 1500 | | 300090 |
| 16 | Св50 | встраиваемый точечный | 1 | 7 | 600 | 44 | 300090 |

## Примечания

1. Ведомости сведены с планов розеток, освещения и выключателей; марки, группы и высоты — те же, что у знаков на планах.
2. Механизмы, рамки и светорегуляторы — одной серии; число постов и клавиш сверено с выбранной серией. Перекрёстная клавиша — отдельный механизм серии.
3. За отметку 0,000 принят уровень чистого пола. Высоты H — от чистого пола до оси изделия; привязки — от чистовой грани стены до оси механизма (у рамки на несколько постов — до оси рамки).
4. Розеточные и мокрые линии — через УЗО или дифавтомат с током утечки не более 30 мА (ПУЭ 7.1.79); в санузле выполнить ДСУП (ПУЭ 7.1.87–7.1.88).
5. Кабель — медный, исполнение нг(A)-LS (ГОСТ 31565-2012); скрытая прокладка только горизонтально и вертикально; фактические трассы зафиксировать исполнительной схемой до закрытия отделок.
6. Расчёт нагрузок, токов КЗ, селективности и сечений — по проекту ЭОМ организации с допуском СРО; лист задаёт состав, расположение и группы.
7. Допущение проекта: кухня: раскладка гарнитура принята проектной, решение автора (ИЗ-12) — мойка М7* у шахты Ш2, ПММ М14* рядом с мойкой, варочная и духовой шкаф в М8*, вытяжка М15**, холодильник М6**; выводы техники — по типовой расстановке; условие: до начала черновых работ сверить раскладку и выводы с чертежом кухни от изготовителя, выводы пересматриваются по его чертежу (вопрос К-8).
8. Допущение проекта: стиральная машина П4* — вертикальной загрузки, габарит в плане 400 × 600 мм (ширина 400 вдоль стены Б); условие закупки, а не пожелание, решение автора (ИЗ-11); машина с фронтальной загрузкой или большего габарита не подходит — перед люком ванна П1; модель не выбрана, габарит и подводку сверить по паспорту до закрытия трасс (вопрос К-19).
9. Марки из допущений, которых нет на этом листе: М7*, М14*, М15** — лист 59; Ш2 — лист 39; П1, П4* — лист 39.
10. Ведомости занимают 2 листов этого наименования: таблицы, не вошедшие в поле листа, продолжены на следующем листе.

Допущения и предложения на листе. Знак «*» принято (замерить). Знак «**» предложено (согласовать). См. лист открытых вопросов (листы 6–11).

| Изм. | Кол.уч | Лист | № док. | Подп. | Дата |
|---|---|---|---|---|---|
| Разраб. | | Кырпан А.С. | | | 05.10.26 |
| Пров. | | | | | |
| ГИП | | | | | |
| | | | | | |
| Н. контр. | | | | | |
| Утв. | | | | | |

**ГД-2026-003-АИ**

Трёхкомнатная квартира

Общая площадь 78,95* м² · * размеры со скана, не замерены (реестр — п. 6–11, К-13)

Дизайн-проект интерьера трёхкомнатной квартиры

| Стадия | Лист | Листов |
|---|---|---|
| РП | 32 | 94 |

Ведомость электроточек и изделий

М 6/м

Кырпан Александр Сергеевич

выпуск 05.10.2026 № 6add39ab8d · стр. 37 из 137

# Ведомость электроточек и изделий (продолжение)

Электроточки, изделия, светильники, клавиши выключателей · б/м

### Расшифровка клавиш

| Марка | Пом. | H, мм | Клав. | Механизм | Группа: светильники |
|---|---|---|---|---|---|
| S1 | 1 | 900 | 1 | проходной | L1: Св1–Св8 |
| | | | 2 | обычный | L2: Св9 |
| S2 | 1 | 800 | 1 | проходной | L1: Св1–Св8 |
| | | | 2 | проходной | L3: Св10, Св11 |
| S3 | 1 | 800 | 1 | перекрёстный | L1: Св1–Св8 |
| | | | 2 | проходной | L3: Св10, Св11 |
| S4 | 4 | 900 | 1 | проходной | L7: Св17–Св22 |
| | | | 2 | обычный | L8: Св23 |
| S5 | 4 | 800 | 1 | перекрёстный | L7: Св17–Св22 |
| | | | 2 | проходной | L9: Св24, Св25 |
| S6 | 4 | 800 | 1 | проходной | L7: Св17–Св22 |
| | | | 2 | проходной | L9: Св24, Св25 |
| S7 | 5 | 900 | 1 | перекрёстный | L10: Св26–Св29, Св53, Св54 |
| S8 | 5 | 900 | 1 | перекрёстный | L10: Св26–Св29, Св53, Св54 |
| S9 | 5 | 900 | 1 | проходной | L10: Св26–Св29, Св53, Св54 |
| | | | 2 | обычный | L11: Св30 |
| S10 | 6 | 900 | 1 | светорегулятор | L12: Св31–Св40 |
| | | | 2 | светорегулятор | L13: Св41 |
| S11** | 6 | 900 | 1 | светорегулятор | L14: Св42**, Св43**, Св44** |
| | | | 2 | светорегулятор | L15: Св45–Св48 |
| S12** | 6 | 900 | 1 | светорегулятор | L16: Св49** |
| S13 | 6 | 900 | 1 | обычный | L17: Св50, Св51 |
| | | | 2 | обычный | L18: Св52 |
| S14 | 8 | 900 | 1 | перекрёстный | L10: Св26–Св29, Св53, Св54 |
| S15 | 8 | 900 | 1 | обычный | L4: Св12–Св14 |
| | | | 2 | обычный | L5: Св15 |
| S16 | 8 | 900 | 1 | обычный | L6: Св16 |
| | | | 2 | проходной | L10: Св26–Св29, Св53, Св54 |

**Допущения и предложения на листе**

Основа листа: размеры сняты со скана плана заказчика по размерным цепочкам, контрольный обмер на объекте не выполнялся (К-13); высота потолка 2700 мм принята: на плане заказчика не указана (К-11); толщины стен приняты: наружные 250 мм, перегородки 150 мм (на плане 85–190 мм) (К-13); разрешённая мощность 15 кВт принята по типовой квартире, технических условий нет (К-14); утолщение стены 190 × 1360 мм и элемент 1470 × 160 мм плана заказчика не определены (К-12); ниши санузла 2 закрыты перегородкой и фальш-стенкой: проектное решение, на плане заказчика ниша у входа открыта (К-18); несущие стены не определены: до технического заключения все существующие стены считаются несущими (К-20); окна существующие и сохраняются; подоконная доска и глубина откосов не заданы — приняты, не замерены (К-27).

Знак «**» — предложение проектировщика, заказчиком не утверждено (согласовать с заказчиком): ИЗ-3: S11, S12 — светорегулятор добавлен разработчиком проекта; Св42, Св43, Св44, Св49 — диммируемость добавлена разработчиком проекта под светорегуляторы S11 и S12.

Открытые вопросы и конфликты по листу: К-7.

Изменения по листу без подписи: ИЗ-15.

См. лист открытых вопросов (лист 6, записи К-7, К-11; лист 7, записи К-12–К-14, К-18, К-20; лист 8, запись К-27; лист 9, запись ИЗ-3; лист 10, запись ИЗ-15).

## Примечания

1. Продолжение ведомостей: лист 2 из 2 этого наименования; таблицы, прерванные на предыдущем листе, продолжены с заголовком «(продолжение)».
2. За отметку 0,000 принят уровень чистого пола. Высоты H — от чистого пола до оси изделия; привязки — от чистовой грани стены до оси механизма (у рамки на несколько постов — до оси рамки).
3. Розеточные и мокрые линии — через УЗО или дифавтомат с током утечки не более 30 мА (ПУЭ 7.1.79); в санузле выполнить ДСУП (ПУЭ 7.1.87–7.1.88).
4. Кабель — медный, исполнение нг(A)-LS (ГОСТ 31565-2012); скрытая прокладка только горизонтально и вертикально; фактические трассы зафиксировать исполнительной схемой до закрытия отделкой.
5. Расчёт нагрузок, токов КЗ, селективности и сечений — по проекту ЭОМ организации с допуском СРО; лист задаёт состав, расположение и группы.

| Изм. | Кол.уч | Лист | № док. | Подп. | Дата |
|---|---|---|---|---|---|
| Разраб. | | Кырлан А.С. | | | 05.10.26 |
| Пров. | | | | | |
| ГИП | | | | | |
| | | | | | |
| Н. контр. | | | | | |
| Утв. | | | | | |

**ГД-2026-003-АИ**

Трёхкомнатная квартира

Общая площадь 78,95* м² · * размеры со скана, не замерены (реестр — п. 6–11, К-13)

Дизайн-проект интерьера трёхкомнатной квартиры

| Стадия | Лист | Листов |
|---|---|---|
| РП | 33 | 94 |

**Ведомость электроточек и изделий (продолжение)**

М б/м

Кырлан Александр Сергеевич

выпуск 05.10.2026 · 6add39ab8d · стр. 38 из 137

# Однолинейная схема щита

Щит квартирный ЩК · без масштаба

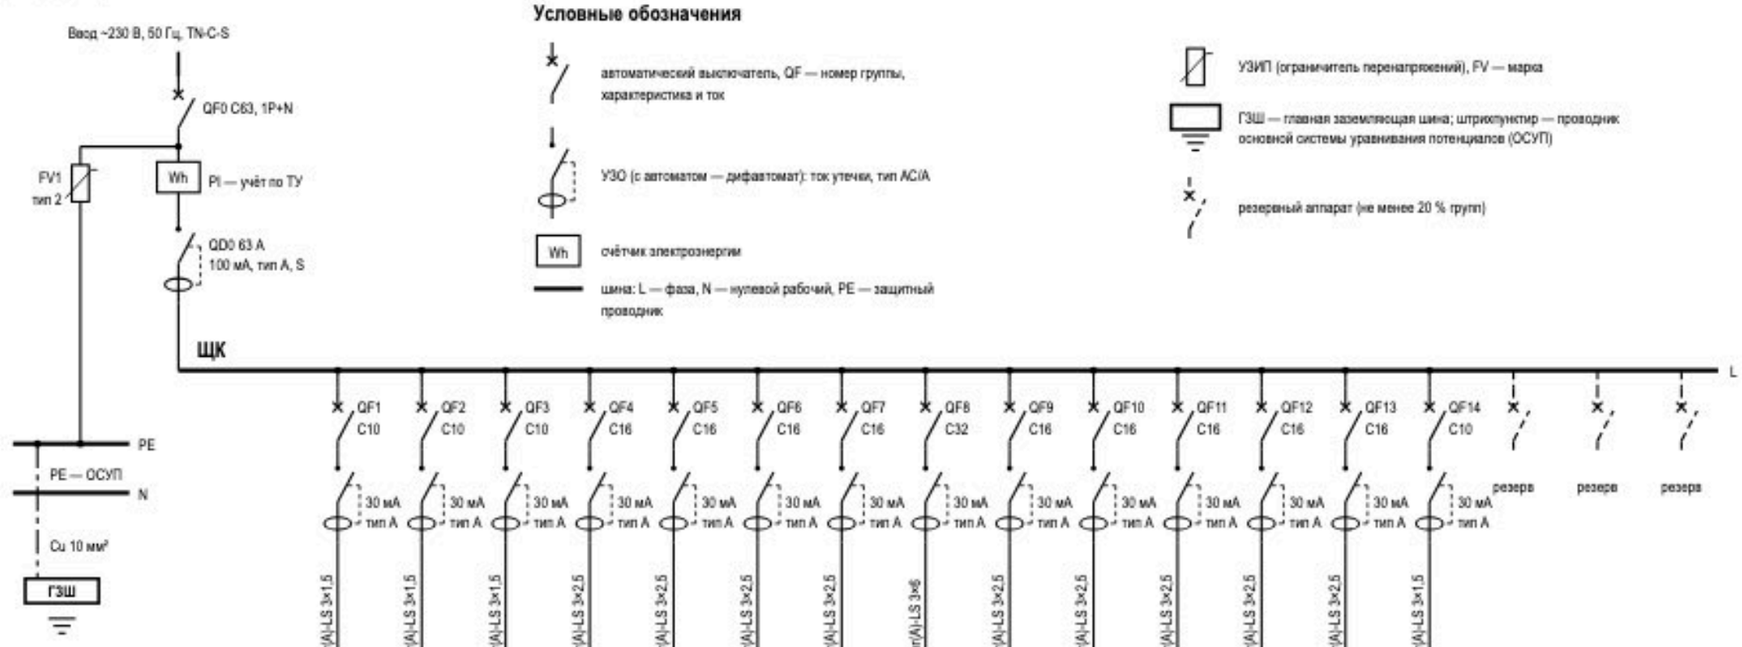


## Условные обозначения

- автоматический выключатель, QF — номер группы, характеристика и ток
- УЗО (с автоматом — дифавтомат): ток утечки, тип AC/A
- Wh — счётчик электроэнергии
- шина: L — фаза, N — нулевой рабочий, PE — защитный проводник
- УЗИП (ограничитель перенапряжений), FV — марка
- ГЗШ — главная заземляющая шина; штрихпунктир — проводник основной системы уравнивания потенциалов (ОСУП)
- резервный аппарат (не менее 20 % групп)

## Данные щитка

| Показатель | Значение |
|---|---|
| Номер щитка | ЩК |
| Тип | ЩРВ-П-48, IP41 |
| Уст. мощность, кВт | 25,85 |
| Разреш. мощность, кВт | 15 |
| Расчётная, кВт | 11,8 |
| Автоматы 1гс занят. / рез. | 14 / 3 |
| Модулей: всего / занято | 48 / 34 |
| Ток на вводе, А | 63 |
| Вводной аппарат | QF0 C63, 1P+N |
| УЗИП | FV1, тип 2, ЩК, после счётчика |
| ГЗШ, проводник ОСУП | Cu 10 мм² |

## Таблица групп щита ЩК и кабельный журнал

| № | Назначение | Помещения | Автомат | УЗО / дифавтомат | Кабель | Длина, м | Р, кВт | Точек |
|---|---|---|---|---|---|---|---|---|
| 1 | освещение спален и гардеробной | 1, 3, 4, 8 | C10 | 30 мА, тип A | ВВГнг(A)-LS 3×1,5 | 45 | 0,5 | 30 |
| 2 | освещение прихожей и кухни-гостиной | 5, 6, 8 | C10 | 30 мА, тип A | ВВГнг(A)-LS 3×1,5 | 50 | 0,5 | 36 |
| 3 | освещение ванной и санузла 2 | 2, 6, 7, 8 | C10 | 30 мА, тип A | ВВГнг(A)-LS 3×1,5 | 25 | 0,05 | 11 |
| 4 | розетки спальни 1 | 1 | C16 | 30 мА, тип A | ВВГнг(A)-LS 3×2,5 | 30 | 1,5 | 6 |
| 5 | розетки спальни 2 | 4 | C16 | 30 мА, тип A | ВВГнг(A)-LS 3×2,5 | 35 | 1,5 | 6 |
| 6 | розетки гостиной и прихожей | 5, 6, 8 | C16 | 30 мА, тип A | ВВГнг(A)-LS 3×2,5 | 40 | 2 | 10 |
| 7 | розетки фартука кухни | 6 | C16 | 30 мА, тип A | ВВГнг(A)-LS 3×2,5 | 25 | 2,5 | 6 |
| 8 | варочная панель | 6 | C32 | 30 мА, тип A | ВВГнг(A)-LS 3×6 | 20 | 7 | 1 |
| 9 | духовой шкаф | 6 | C16 | 30 мА, тип A | ВВГнг(A)-LS 3×2,5 | 20 | 3 | 1 |
| 10 | посудомоечная машина | 6 | C16 | 30 мА, тип A | ВВГнг(A)-LS 3×2,5 | 20 | 2 | 1 |
| 11 | холодильник и вытяжка | 6 | C16 | 30 мА, тип A | ВВГнг(A)-LS 3×2,5 | 22 | 0,6 | 2 |
| 12 | стиральная машина | 2 | C16 | 30 мА, тип A | ВВГнг(A)-LS 3×2,5 | 15 | 2,2 | 1 |
| 13 | розетки ванной и санузла 2 (фен), полотенцесушители | 2, 7 | C16 | 30 мА, тип A | ВВГнг(A)-LS 3×2,5 | 25 | 2,4 | 4 |
| 14 | слаботочный щит (роутер, ONT) | 5 | C10 | 30 мА, тип A | ВВГнг(A)-LS 3×1,5 | 5 | 0,1 | 1 |
| | Итого по сечениям ВВГнг(A)-LS, м: 3×1,5 — 125; 3×2,5 — 232; 3×6 — 20 | | | | | 377 | | |

**Допущения и предложения на листе**

Основа листа: размеры сняты со скана плана заказчика по размерным цепочкам, контрольный обмер на объекте не выполнялся (К-13); высота потолка 2700 мм принята: на плане заказчика не указана (К-11); толщины стен приняты: наружные 250 мм, перегородки 150 мм (на плане 85–190 мм) (К-13); разрешённая мощность 15 кВт принята по типовой квартире, технических условий нет (К-14); утолщение стены 190 × 1360 мм и элемент 1470 × 160 мм плана заказчика не определены (К-12); ниши санузла 2 закрыты перегородкой и фальш-стеной: проектное решение, на плане заказчика ниша у входа открыта (К-18); несущие стены не определены: до технического заключения все существующие стены считаются несущими (К-20); окна существующие и сохраняются; подоконная доска и глубина откосов не заданы — приняты, не замерены (К-27).

Открытые вопросы и конфликты по листу: К-14.

См. лист открытых вопросов (лист 6, запись К-11; лист 7, записи К-12–К-14, К-18, К-20; лист 8, запись К-27).

## Примечания

1. Схема однолинейная: одна линия — фаза, N и PE группы; аппараты — в отключённом положении (ГОСТ 2.702, ГОСТ 2.755). Номера групп — как у точек на планах (гр.). За отметку 0,000 принят уровень чистого пола; высота щита — по плану розеток.
2. Розеточные и мокрые линии — через УЗО или дифавтомат с током утечки не более 30 мА (ПУЭ 7.1.79); в санузле выполнить ДСУП (ПУЭ 7.1.87–7.1.88).
3. УЗО тип A — для линий с электроникой, стиральной и посудомоечной машиной, LED-драйверами; тип AC — только для чисто активной нагрузки.
4. Кабель — медный, исполнение нг(A)-LS (ГОСТ 31565-2012); скрытая прокладка только горизонтально и вертикально, фактические трассы зафиксировать исполнительной схемой до закрытия отделкой.
5. Номинал автомата — не выше допустимого тока кабеля: 1,5 мм² — до 10 А, 2,5 мм² — до 16 А. Резерв щита — не менее 20 % модулей.
6. Расчёт нагрузок, токов КЗ, селективности и сечений — по проекту ЭОМ организации с допуском СРО; лист задаёт состав, расположение и группы.
7. УЗИП FV1 — после вводного автомата, проводник к шине PE — кратчайший, без петель. Шина PE щита соединяется с ГЗШ проводником ОСУП; к ГЗШ присоединяются трубы водопровода и отопления на вводе в квартиру (ПУЭ 7.1.87). Шины N и PE — раздельные, после разделения PEN не объединяются.
8. До подключения нагрузки — приёмо-сдаточные испытания с протоколом: сопротивление изоляции линий не менее 0,5 МОм, срабатывание УЗО по току и времени, непрерывность защитных проводников PE (ПУЭ, гл. 1.8).

| Изм. | Кол.уч | Лист | № док. | Подп. | Дата |
|---|---|---|---|---|---|
| Разраб. | | Кырпан А.С. | | | 05.10.26 |
| Пров. | | | | | |
| ГИП | | | | | |
| Н. контр. | | | | | |
| Утв. | | | | | |

**ГД-2026-003-АИ**

Трёхкомнатная квартира

Общая площадь 78,95* м² · * размеры со скана, не замерены (реестр — п. 6–11, К-13)

Дизайн-проект интерьера трёхкомнатной квартиры

| Стадия | Лист | Листов |
|---|---|---|
| РП | 34 | 94 |

**Однолинейная схема щита**

М 6/м

Кырпан Александр Сергеевич

выпуск 05.10.2026 · 6add39ab8d · стр. 39 из 137

# План принципиальных трасс

Силовые трассы и объёмы электромонтажа, слаботочка в объёмах · размеры в мм

ПРЕДВАРИТЕЛЬНО · не для производства работ · открыто пунктов: 31 (реестр — л. 6–11)

**Допущения и предложения на листе**

Основа листа: размеры сняты со скана плана заказчика по размерным цепочкам, контрольный обмер на объекте не выполнялся (К-13); высота потолка 2700 мм принята: на плане заказчика не указана (К-11); толщины стен приняты: наружные 250 мм, перегородки 150 мм (на плане 85–190 мм) (К-13); разрешённая мощность 15 кВт принята по типовой квартире, технических условий нет (К-14); утолщение стены 190 × 1360 мм и элемент 1470 × 160 мм плана заказчика не определены (К-12); ниши санузла 2 закрыты перегородкой и фальш-стеной: проектное решение, на плане заказчика ниша у входа открыта (К-18); несущие стены не определены: до технического заключения все существующие стены считаются несущими (К-20); окна существующие и сохраняются; подоконная доска и глубина откосов не заданы — приняты, не замерены (К-27).

Знак «*» — принято, не замерено и не подтверждено (замерить на объекте): К-17: Ст К1-1, Ст В1-1, Ст К1-2, Ст В1-2; К-25: дверь пом. 8 (стена А) — толщина стены в проёме принята 150 мм (как у всех перегородок модели), по скану плана заказчика стена 85 мм — не замерено (К-25); проём существующий, скрытый блок ставится в него с зазором 10–15 мм на сторону, полотно уже проёма; узел скрытой двери выполнен для принятой толщины 150 мм; К-26: дверь пом. 5 (стена В) — входная дверь существующая; по плану заказчика полотно открывается наружу, в общий коридор — направление взято с плана и на объекте не проверено; остаётся ли существующий блок или он заменяется — не решено (К-26).

Знак «**» — предложение проектировщика, заказчиком не утверждено (согласовать с заказчиком): И3-17: ЩС — щит слаботочный: место и состав.

Изменения по листу без подписи: И3-17.

См. лист открытых вопросов (лист 6, запись К-11; лист 7, записи К-12–К-14, К-17, К-18, К-20; лист 8, записи К-25–К-27; лист 11, запись И3-17).

## Кабель по группам ВВГнг(А)-LS, м

| Гр. | мм² | Трасса | Данные |
|---|---|---|---|
| 1 | 3×1,5 | 94,3 | 45 |
| 2 | 3×1,5 | 93,4 | 50 |
| 3 | 3×1,5 | 58,2 | 25 |
| 4 | 3×2,5 | 31,1 | 30 |
| 5 | 3×2,5 | 29,1 | 35 |
| 6 | 3×2,5 | 52,1 | 40 |
| 7 | 3×2,5 | 28,2 | 25 |

| Гр. | мм² | Трасса | Данные |
|---|---|---|---|
| 8 | 3×6 | 15,4 | 20 |
| 9 | 3×2,5 | 15,5 | 20 |
| 10 | 3×2,5 | 14,4 | 20 |
| 11 | 3×2,5 | 14,2 | 22 |
| 12 | 3×2,5 | 13,2 | 15 |
| 13 | 3×2,5 | 31,9 | 25 |
| 14 | 3×1,5 | 3,6 | 5 |
| **Σ** | | **494,6** | **377** |

## Экспликация помещений

| № | Помещение | Площадь, м² |
|---|---|---|
| 1 | Спальня 1 | 17,75 |
| 2 | Ванная | 4,43 |
| 3 | Гардеробная | 1,85 |
| 4 | Спальня 2 | 12,80 |
| 5 | Прихожая | 7,13 |
| 6 | Кухня-гостиная | 29,20 |
| 7 | Санузел 2 | 2,29 |
| 8 | Коридор | 3,50 |
| | Итого (общая площадь) | 78,95 |

## Объёмы прокладки

| Работа, материал | Ед. | Кол. |
|---|---|---|
| Гофротруба Ø20 в потолочном пространстве | м | 197,5 |
| Кабель-канал плинтуса для силовых линий | м | 127,3 |
| Короб или накладной канал для вертикальных спусков и подъёмов | м | 87,2 |
| Коробка распределительная (РК) над дверью помещения | шт | 8 |
| Слаботочка: кабель домофона | м | 2,9 |
| Слаботочка: Кабель коаксиальный RG-6 (75 Ом) к розеткам ТВ | м | 29,1 |
| Слаботочка: U/UTP кат. 6 (LAN, Wi-Fi, камеры) | м | 61,2 |
| Слаботочка: гофротруба Ø20 отдельно от силовых | м | 83,9 |

## Штробы — только после заключения

| Работа | Ед. | Кол. |
|---|---|---|
| Вертикальные штробы 20×20 мм от потолка до каждой настенной точки (в маршрут без штроб не входят) | м | 103,22 |

## Условные обозначения

- ЩК — щит квартирный
- РК — распределительная коробка над дверью помещения
- магистраль от щита к РК: потолочное пространство, гофра
- мебель и сантехприборы — подложка

## Примечания

1. За отметку 0,000 принят уровень чистого пола. Высоты Н — от чистого пола до оси изделия; привязки — от чистовой грани стены до оси механизма (у рамки на несколько постов — до оси рамки).
2. Розеточные и мокрые линии — через УЗО или дифавтомат с током утечки не более 30 мА (ПУЭ 7.1.79); в санузле выполнить ДСУП (ПУЭ 7.1.87–7.1.88).
3. Кабель — медный, исполнение нг(А)-LS (ГОСТ 31565-2012); скрытая прокладка только горизонтально и вертикально, фактические трассы зафиксировать исполнительной схемой до закрытия отделкой.
4. Расчёт нагрузок, токов КЗ, селективности и сечений — по проекту ЭОМ организации с допуском СРО; лист задаёт состав, расположение и группы.
5. Длины — по плану: от щита вверх в потолочное пространство, по дверям и коридору без захода в мокрые помещения к распределительной коробке над дверью, далее к точкам; вертикали считаются вниз и обратно (у последней точки цепочки — в один конец); запас 10 %. Трассы принципиальные: фактическую зафиксировать исполнительной схемой до закрытия отделкой.
6. Несущие стены не определены: штробы в стенах не выполнять. Маршрут проложен без штроб: горизонтали — за потолком в гофре (197,5 м) и в кабель-канале плинтуса (127,3 м), вертикали — в коробе или накладном канале (153,4 м кабеля). Точек: за потолком — 50, спуск из потолка — 14, по плинтусу — 15, плинтус и подъём 37.
7. Вариант со штробами — работа после технического заключения: 103,22 м вертикальных штроб от потолка до каждой настенной точки; условие — только после технического заключения: стена не несущая (или вертикальная штроба в несущей согласована конструктором), глубина и ширина 20–25 мм, не в зонах 0–2 ванной. Без заключения и согласования конструктора в смету и в график эта работа не входит.
8. В данных проекта (журнал щита) длины кабеля внесены оценкой (377 м), по трассам из геометрии — 495 м (+31 %): к закупке и в смету принимать длины по трассам, а оценку в данных проекта заменить.
9. Слаботочные сети: кабели и точки считаются по лучам от ЩС** (лист слаботочных сетей): 93 м, портов патч-панели и коммутатора не менее 5; из точек 2 предложения листа слаботочки, не подтверждённые заказчиком. Изделия — в ведомости изделий.

1000 мм · печать 1:1

| Изм. | Кол.уч | Лист | № док. | Подп. | Дата |
|---|---|---|---|---|---|
| Разраб. | | Кырпан А.С. | | | 05.10.26 |
| Пров. | | | | | |
| ГИП | | | | | |
| | | | | | |
| Н. контр. | | | | | |
| Утв. | | | | | |

**ГД-2026-003-АИ**

Трёхкомнатная квартира

Общая площадь 78,95* м² · * размеры со скана, не замерены (реестр — п. 6–11, К-13)

Дизайн-проект интерьера трёхкомнатной квартиры

| Стадия | Лист | Листов |
|---|---|---|
| РП | 35 | 94 |

**План принципиальных трасс**

М 1:100

Кырпан Александр Сергеевич

выпуск 05.10.2026 № 6add39ab8d · стр. 40 из 137

# План слаботочных сетей

Интернет, ТВ, домофон · размеры в мм · высоты от чистого пола

ПРЕДВАРИТЕЛЬНО · не для производства работ · открыто пунктов: 31 (реестр — л. 6–11)

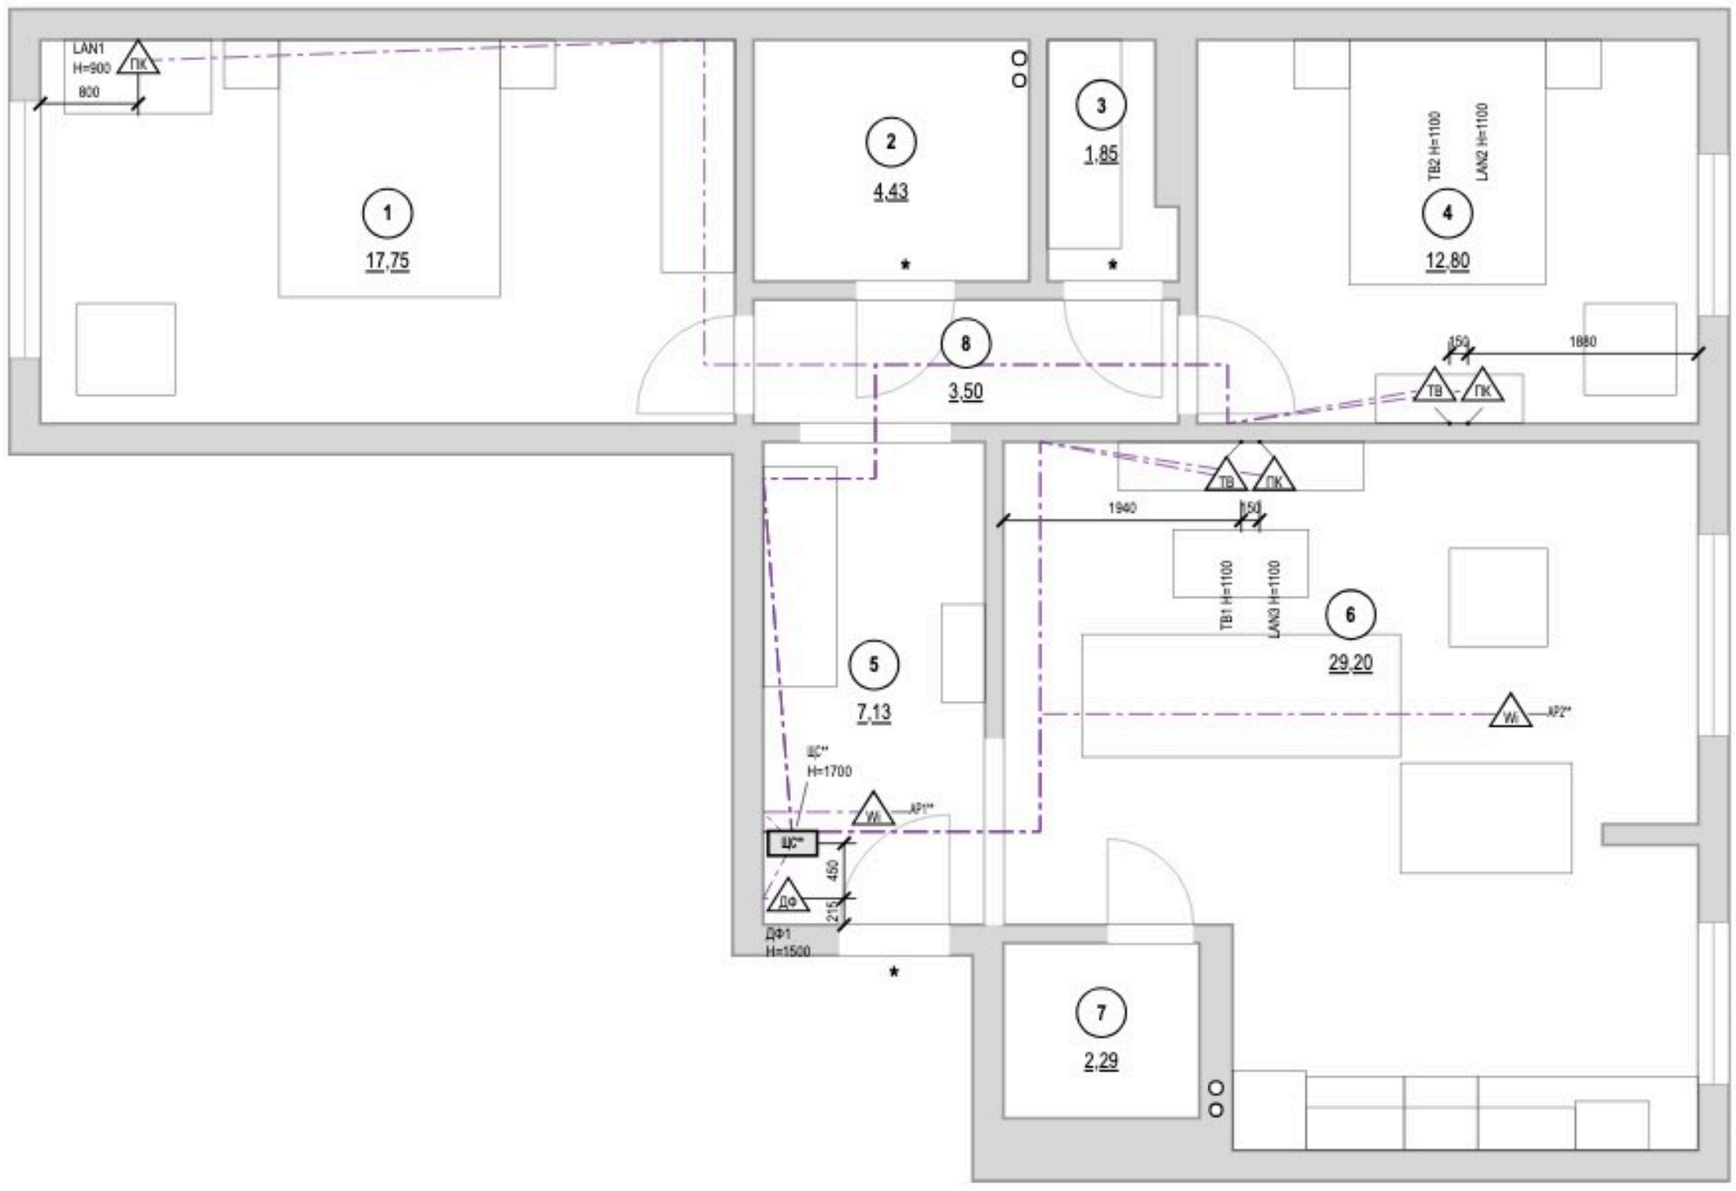


## Ведомость слаботочных точек

| Марка | Пом. | Назначение | H, мм | Кабель |
|---|---|---|---|---|
| LAN1 | 1 | розетка LAN (RJ45) | 900 | U/UTP кат. 6 |
| TB2 | 4 | розетка ТВ | 1100 | RG-6 |
| LAN2 | 4 | розетка LAN (RJ45) | 1100 | U/UTP кат. 6 |
| ЩС** | 5 | щит слаботочный | 1700 | ввод прав. |
| ДФ1 | 5 | домофон (трубка) | 1500 | по системе |
| AP1** | 5 | точка доступа Wi-Fi | | U/UTP кат. 6 |
| TB1 | 6 | розетка ТВ | 1100 | RG-6 |
| LAN3 | 6 | розетка LAN (RJ45) | 1100 | U/UTP кат. 6 |
| AP2** | 6 | точка доступа Wi-Fi | | U/UTP кат. 6 |

## Условные обозначения

- ЩС — щит слаботочный: ввод провайдера, роутер, коммутатор
- ПК — розетка компьютерная RJ45
- ТВ — розетка телевизионная
- ДФ — трубка или монитор домофона
- Wi — точка доступа Wi-Fi (питание PoE)
- кабель от ЩС до точки, отдельным лучом
- мебель и сантехприборы — подложка
- (1) — номер помещения, площадь м²

Допущения и предложения на листе. Основа листа: размеры сняты со скана плана заказчика по размерным цепочкам, контрольный обмер на объекте не выполнялся (К-13); высота потолка 2700 мм принята: на плане заказчика не указана (К-11); толщины стен приняты: наружные 250 мм, перегородки 150 мм (на плане 85–190 мм) (К-13); разрешённая мощность 15 кВт принята по типовой квартире, технических условий нет (К-14); утопление стены 190 × 1360 мм и элемент 1470 × 160 мм плана заказчика не определены (К-12); ниши санузла 2 закрыты перегородкой и фальш-стеной: проектное решение, на плане заказчика ниша у входа открыта (К-18); несущие стены не определены: до технического заключения все существующие стены считаются несущими (К-20); окна существующие и сохраняются; подоконная доска и глубина откосов не заданы — приняты, не замерены (К-27). Знак «*» — принято, не замерено и не подтверждено (замерить на объекте): К-17: Ст К1-1, Ст В1-1, Ст К1-2, Ст В1-2. Знак «**» — предложение проектировщика, заказчиком не утверждено (согласовать с заказчиком): ИЗ-17: AP1, AP2 — точка доступа Wi-Fi: число и места; ЩС — щит слаботочный: место и состав. См. лист открытых вопросов (лист 6, запись К-11; лист 7, записи К-12–К-14, К-17, К-18, К-20; лист 8, записи К-25–К-27; лист 11, запись ИЗ-17); по листу — ИЗ-17.

## Примечания

1. За отметку 0,000 принят уровень чистого пола. Высоты H — от чистого пола до оси изделия; привязки — от чистовой грани стены до оси механизма (у рамки на несколько постов — до оси рамки).
2. Высота установки, не указанная на плане: розетки LAN и ТВ — 300 мм от чистого пола.
3. Слаботочные кабели — отдельно от силовых: в своей трубе или лотке, при параллельной прокладке не ближе 100 мм к силовым, пересечения под прямым углом; каждую точку — отдельным кабелем от ЩС** без скруток.
4. Трассы на листе — принципиальные; фактические зафиксировать исполнительной схемой до закрытия отделкой. Силовые линии, УЗО 30 мА, ДСУП, кабель нг(A)-LS — по листам розеток и щита.
5. Проект силовой части и расчёт токов КЗ — по проекту ЭОМ; слаботочная часть согласуется с провайдером и управляющей компанией (домофон, коллективное ТВ).

1000 мм · печать 1:1

| Изм. | Кол.уч | Лист | № док. | Подп. | Дата |
|---|---|---|---|---|---|
| Разраб. | | Кырпан А.С. | | | 05.10.26 |
| Пров. | | | | | |
| ГИП | | | | | |
| | | | | | |
| Н. контр. | | | | | |
| Утв. | | | | | |

**ГД-2026-003-АИ**

Трёхкомнатная квартира

Общая площадь 78,95* м² · * размеры со скана, не замерены (реестр — п. 6–11, К-13)

Дизайн-проект интерьера трёхкомнатной квартиры

| Стадия | Лист | Листов |
|---|---|---|
| РП | 36 | 94 |

**План слаботочных сетей**

М 1:50

Кырпан Александр Сергеевич

выпуск 05.10.2026 № 6add39ab8d · стр. 41 из 137

04

# Отопление и вентиляция

Кырлан Александр Сергеевич

выпуск 05.10.2026 № 6add39ab8d - стр. 42 из 137

# План вентиляции

Вытяжка, приток, переток · кондиционирование не предусмотрено · размеры в мм · высоты от чистого пола

ПРЕДВАРИТЕЛЬНО · не для производства работ · открыто пунктов: 31 (реестр — л. 6–11)

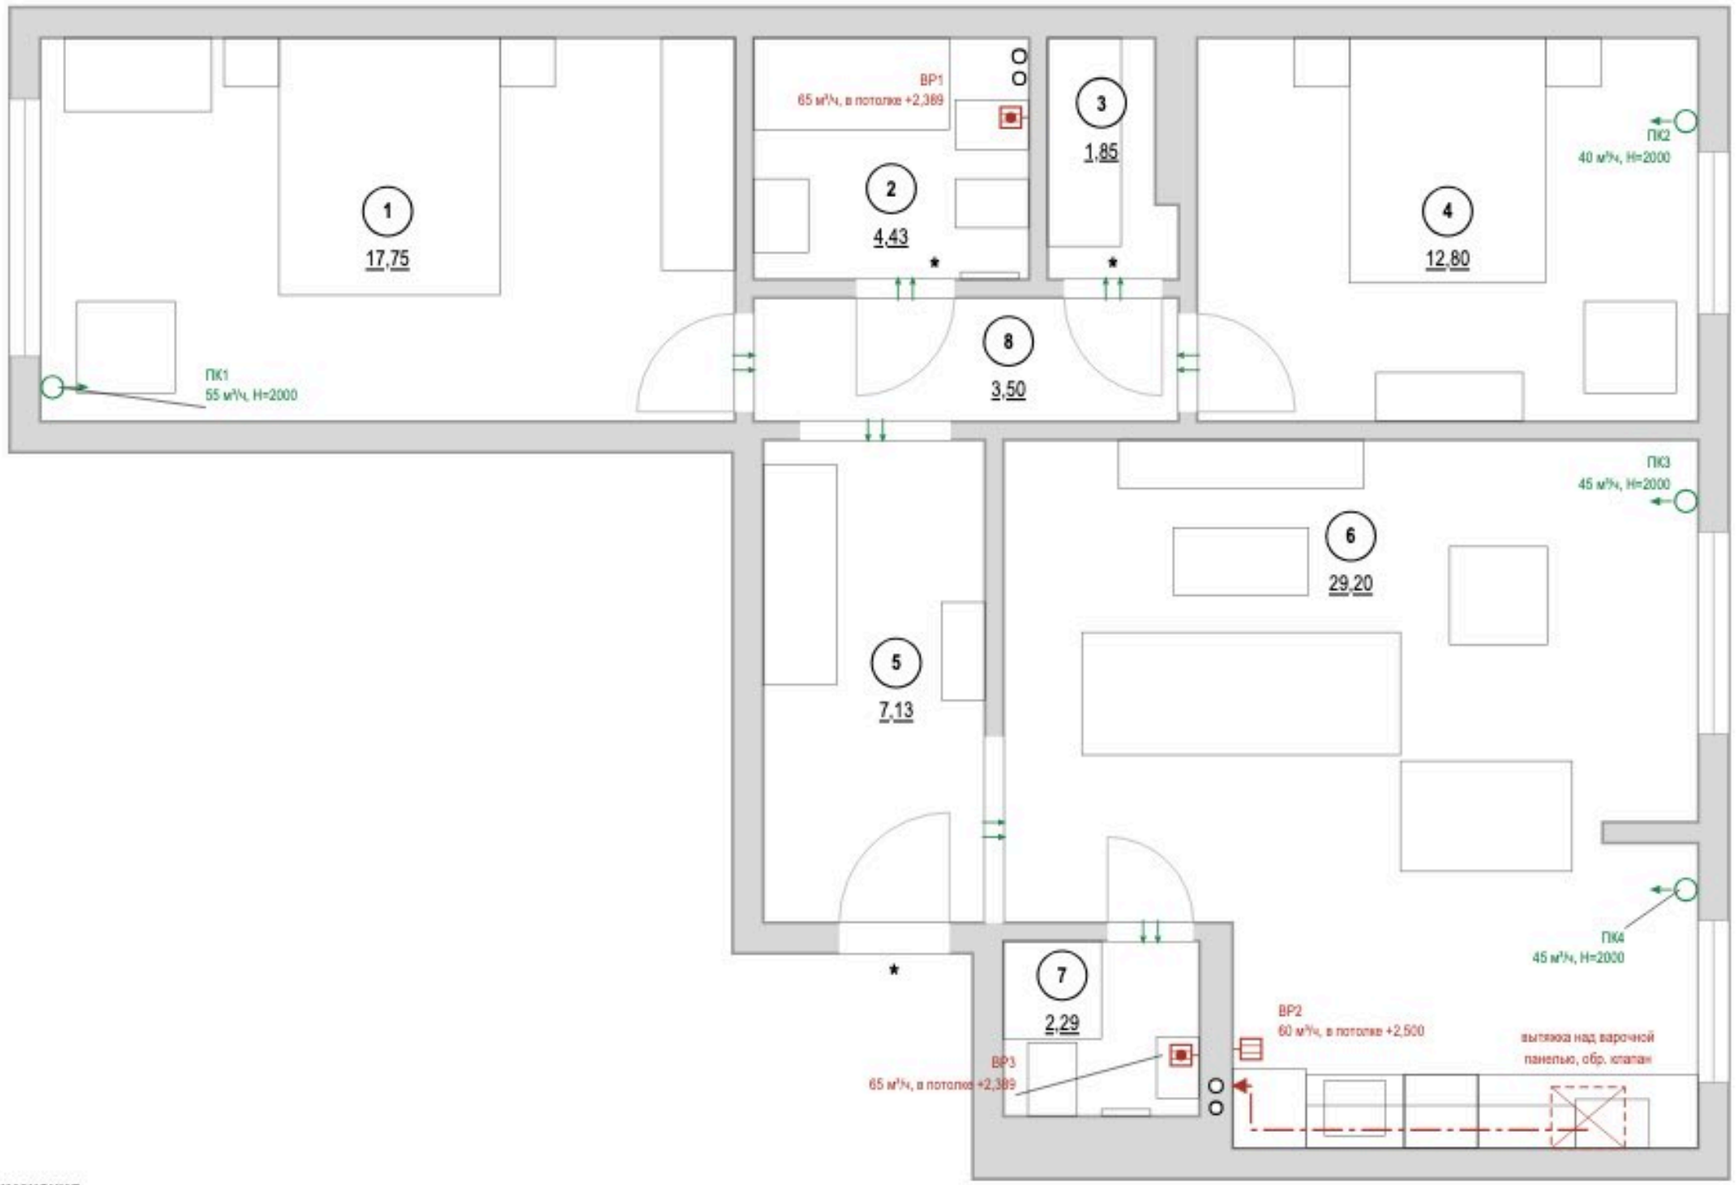


## Условные обозначения

- ○ стояк К1 — канализация, В1 — ХВС, Т3 — ГВС
- (1) номер помещения, площадь м²
- вытяжная решётка в подшивном потолке, воздуховод за потолком до канала
- вентилятор с обратным клапаном в подшивном потолке, воздуховод за потолком до канала
- ○→ приточный клапан (КИВ) в наружной стене: марка, расход, Н центра
- переток: зазор под полотном или переточная решётка
- кухонная вытяжка над варочной панелью
- воздуховод кухонной вытяжки в коробе под потолком
- ▶ отдельный вход воздуховода в вентканал, обратный клапан
- * «*» — принято, не замерено и не подтверждено

## Воздухообмен, м³/ч

| № | Помещение | Выт. норма | Выт. проект | Прит. норма | Прит. проект | Устройства |
|---|---|---|---|---|---|---|
| 1 | Спальня 1 | | | 54 | 55 | ПК1 |
| 2 | Ванная | 50 | 65 | | | ВР1 |
| 3 | Гардеробная | 1 | | | | переток |
| 4 | Спальня 2 | | | 39 | 40 | ПК2 |
| 6 | Кухня-гостиная | 60 | 60 | 88 | 90 | ВР2, ПК3, ПК4 |
| 7 | Санузел 2 | 50 | 65 | | | ВР3 |
| | **Итого** | **161** | **190** | **181** | **185** | |

Воздухообмен квартиры — по большей из сумм притока и вытяжки: норма 181 м³/ч, проект 190 м³/ч.
Вытяжка не меньше притока — баланс сведён.

**Привязки — до обмера**
Вентканалы в исходных данных не заданы: решётки и вход вытяжки показаны у стояков К1 (вентблок у мокрой зоны). До черновых работ — обмер каналов и проверка тяги; лист перевыпустить по факту.

## Примечания

1. Расчёт систем ОВ и подбор оборудования — проектная организация с допуском СРО; лист даёт места, трассы и привязки.
2. Нормы вытяжки — СП 54.13330.2022 (Изм. 1, 2), табл. 7.1: кухня с электроплитой 60 м³/ч, с газовой 100; ванная и совмещённый санузел 50; уборная 25; гардеробная 0,2 ч⁻¹. Приток в жилые — 3 м³/ч на 1 м² (менее 20 м² общей площади на человека), иначе 30 м³/ч на человека.
3. Вентканалы и шахты не сужать, не переносить и не закрывать; вентилятор и кухонная вытяжка — через обратный клапан, без перекрытия естественной тяги.
4. Проектные расходы — не ниже нормы, вытяжка сведена с притоком вентиляторами мокрых помещений. Клапаны — в простенке у окна, центр 2000 мм, не над кроватью, не ближе 300 мм к стоякам отопления; типоразмер — на расход.
5. Под подшивным потолком вытяжка — в потолке, воздуховодом за потолком до канала. Кухонная вытяжка в воздухообмен не включена: воздуховод не менее Ø125 в коробе, вход в канал отдельный.
6. Переток — зазор под полотнами межкомнатных дверей или переточная решётка.
7. Кондиционирование заданием не предусмотрено; при установке трассы фреона и дренажа (не менее 40 мм/м, в К1 через сифон) и питание заложить до черновых работ.
8. Привязки оборудования — по паспортам приобретённых моделей, до черновых работ.
9. Знак «*» у проёма — допущение: положение проёма не замерено (дверь пом. 5, стена В; дверь пом. 8, стена А (2 шт.)); размер напечатан как принятый. Реестр: листы 6–11, вопросы К-26, К-25.

1000 мм · печать 1:1

Допущения и предложения на листе. Знак «*» принято (замерить): Ст К1-1, Ст В1-1, Ст К1-2, Ст В1-2. См. лист открытых вопросов (листы 6–11).

| Изм. | Кол.уч | Лист | № док. | Подп. | Дата |
|---|---|---|---|---|---|
| Разраб. | | Кырпан А.С. | | | 05.10.26 |
| Пров. | | | | | |
| ГИП | | | | | |
| Н. контр. | | | | | |
| Утв. | | | | | |

**ГД-2026-003-АИ**

Трёхкомнатная квартира

Общая площадь 78,95* м² · * размеры со скана, не замерены (реестр — л. 6–11, К-13)

Дизайн-проект интерьера трёхкомнатной квартиры

| Стадия | Лист | Листов |
|---|---|---|
| РП | 37 | 94 |

**План вентиляции**

М 1:50

Кырпан Александр Сергеевич

выпуск 05.10.2026 · 6add39ab8d · стр. 43 из 137

# План отопления

Радиаторы, стояки, подводки · размеры в мм · высоты от чистого пола

ПРЕДВАРИТЕЛЬНО · не для производства работ · открыто пунктов: 31 (реестр — л. 6–11)

## Условные обозначения

- (1) — номер помещения, площадь м²
- радиатор отопления (марка РО-N, длина по плану)
- (Т) — клапан с термоголовкой на подаче
- стояк отопления, подающий (Ст Т1-N)
- стояк отопления, обратный (Ст Т2-N)
- Т1 — отопление, подающий трубопровод
- Т2 — отопление, обратный трубопровод
- * — «*» — принято, не замерено и не подтверждено

## Ведомость радиаторов

| Марка | Помещение | Тип | Д×В×Г, мм | Низ / стена | Q, Вт |
|---|---|---|---|---|---|
| РО-1 | 1. Спальня 1 | панельный* | 1400×600×100 | 120 / 40 | расч. |
| РО-2 | 4. Спальня 2 | панельный* | 900×600×100 | 120 / 40 | расч. |
| РО-3 | 6. Кухня-гостиная | панельный* | 1100×600×100 | 120 / 40 | расч. |
| РО-4 | 6. Кухня-гостиная | панельный* | 900×600×100 | 120 / 40 | расч. |

* тип и мощность — по теплотехническому расчёту
Низ — от чистого пола, стена — зазор до задней панели, мм.

**Привязки — до обмера**

Стояки отопления в исходных данных не заданы: показаны у откосов окон, подводки — принципиально. До черновых работ — обмер стояков и паспорта приборов; лист перевыпустить по факту.

Допущения и предложения на листе. Основа листа: размеры сняты со скана плана заказчика по размерным цепочкам, контрольный обмер на объекте не выполнялся (К-13); высота потолка 2700 мм принята: на плане заказчика не указана (К-11); толщины стен приняты: наружные 250 мм, перегородки 150 мм (на плане 85–190 мм) (К-13); разрешённая мощность 15 кВт принята по типовой квартире, технических условий нет (К-14); утолщение стены 190 × 1360 мм и элемент 1470 × 160 мм плана заказчика не определены (К-12); ниши санузла 2 закрыты перегородкой и фальш-стеной: проектное решение, на плане заказчика ниша у входа открыта (К-18); несущие стены не определены: до технического заключения все существующие стены считаются несущими (К-20); окна существующие и сохраняются; подоконная доска и глубина откосов не заданы — приняты, не замерены (К-27). Знак «*» — принято, не замерено и не подтверждено (замерить на объекте). См. лист открытых вопросов (лист 6, запись К-11; лист 7, записи К-12–К-14, К-18, К-20; лист 8, записи К-25–К-27).

## Примечания

1. Расчёт системы отопления, теплопотерь и подбор приборов — проектная организация с допуском СРО; лист даёт места и привязки.
2. Тип, длина и мощность радиаторов — по теплотехническому расчёту; лист задаёт места, зазоры и подключение.
3. Радиаторы — под каждым окном жилых комнат и кухни, центр по оси проёма, длина 0,7 ширины окна (кратно 100); окончательно — по расчёту.
4. Зазоры радиатора: низ не менее 100 мм от чистого пола, верх не менее 100 мм до подоконника, 30–50 мм от стены до задней панели; центр по оси окна с допуском ±20 мм.
5. Радиаторы не закрывать глухими коробами и мебелью; перенос и замена приборов в многоквартирном доме — переустройство, согласование с управляющей организацией (ЖК РФ ст. 25–26); вынос на лоджию запрещён.
6. Трубы отопления через межквартирные стены не прокладывать (СП 51.13330.2011, п. 9.19); через перекрытия и перегородки — в гильзах.
7. Привязки приборов и подводок — по паспортам приобретённых радиаторов и клапанов, до черновых работ.
8. До закрытия отделкой трубопроводы отопления испытать гидростатическим давлением с оформлением акта (СП 73.13330.2016, 7.2–7.3).
9. Знак «*» у проёма — допущение: положение проёма не замерено (дверь пом. 5, стена В; дверь пом. 8, стена А (2 шт.)); размер напечатан как принятый. Реестр: листы 6–11, вопросы К-26, К-25.

1000 мм · печать 1:1

| Изм. | Кол.уч | Лист | № док. | Подп. | Дата |
|---|---|---|---|---|---|
| Разраб. | | Кырпан А.С. | | | 05.10.26 |
| Пров. | | | | | |
| ГИП | | | | | |
| | | | | | |
| Н. контр. | | | | | |
| Утв. | | | | | |

**ГД-2026-003-АИ**

Трёхкомнатная квартира

Общая площадь 78,95* м² · * размеры со скана, не замерены (реестр — п. 6–11, К-13)

Дизайн-проект интерьера трёхкомнатной квартиры

| Стадия | Лист | Листов |
|---|---|---|
| РП | 38 | 94 |

**План отопления**

М 1:50

Кырпан Александр Сергеевич

выпуск 05.10.2026 · 6add39ab8d · стр. 44 из 137

05

# Водоснабжение и канализация

Кырлан Александр Сергеевич

выпуск 05.10.2026 № 6add39ab8d · стр. 45 из 137

# План выводов сантехники

Выводы В1, Т3, К1 · привязки от чистовых стен · высоты от чистого пола, мм

ПРЕДВАРИТЕЛЬНО · не для производства работ · открыто пунктов: 31 (реестр — л. 6–11)

### Фрагмент 1. Ванная (пом. 2)

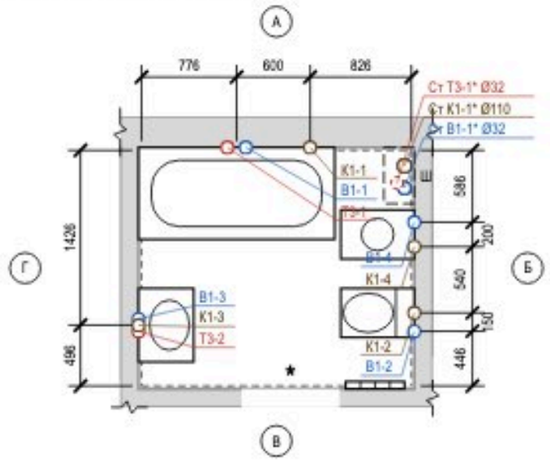


### Фрагмент 2. Кухня-гостиная (пом. 6)

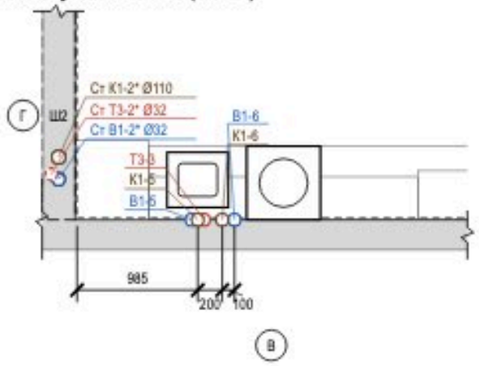


### Фрагмент 3. Санузел 2 (пом. 7)

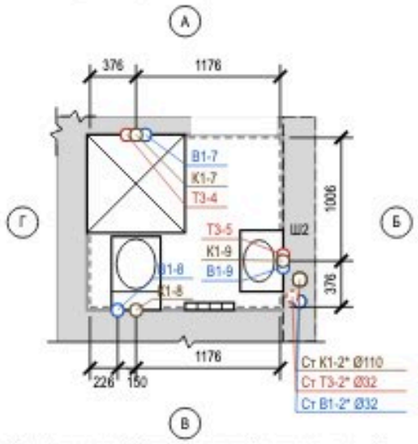


**Допущения и предложения на листе**

Основа листа: размеры сняты со скана плана заказчика по размерным цепочкам, контрольный обмер на объекте не выполнялся (К-13); высота потолка 2700 мм принята: на плане заказчика не указана (К-11); толщины стен приняты: наружные 250 мм, перегородки 150 мм (на плане 85–190 мм) (К-13); разрешённая мощность 15 кВт принята по типовой квартире, технических условий нет (К-14); утолщение стены 190 × 1360 мм и элемент 1470 × 160 мм плана заказчика не определены (К-12); ниши санузла 2 закрыты перегородкой и фальш-стеной: проектное решение, на плане заказчика ниша у входа открыта (К-18); несущие стены не определены: до технического заключения все существующие стены считаются несущими (К-20); окна существующие и сохраняются; подоконная доска и глубина откосов не заданы — приняты, не замерены (К-27).

Знак «*» — принято, не замерено и не подтверждено (замерить на объекте): ИЗ-11, К-19: П4 — вертикальная загрузка 400 × 600 мм — условие закупки (решение автора, ИЗ-11); модель не выбрана, габарит сверить по паспорту; К-8: М7, М14, М8, П11, П12; К-17: Ст К1-1, Ст В1-1, Ст К1-2, Ст В1-2; К-25: дверь пом. 8 (стена А) — толщина стены в проёме принята 150 мм (как у всех перегородок модели), по скану плана заказчика стена 85 мм — не замерено (К-25); проём существующий, скрытый блок ставится в него с зазором 10–15 мм на сторону, полотно уже проёма; узел скрытой двери выполнен для принятой толщины 150 мм.

Знак «**» — предложение проектировщика, заказчиком не утверждено (согласовать с заказчиком): ИЗ-5, К-8: М6, М15.

Открытые вопросы и конфликты по листу: К-1, К-5, К-17–К-19.

Изменения по листу без подписи: ИЗ-16.

См. лист открытых вопросов (лист 6, записи К-1, К-5, К-8, К-11; лист 7, записи К-12–К-14, К-17–К-20; лист 8, записи К-25, К-27; лист 9, запись ИЗ-5; лист 10, записи ИЗ-11, ИЗ-16).

### Ведомость привязок выводов

| Код | Прибор | Ø | H, мм | Привязка от чист. стен, мм | Прим. |
|---|---|---|---|---|---|
| В1-1 | П1 ванна | ½" | 800* | ст. А: 851 от Г | межос. 150 |
| Т3-1 | П1 ванна | ½" | 800* | ст. А: 701 от Г | межос. 150 |
| К1-1 | П1 ванна | Ø50 | 50* | ст. А: 826 от Б | |
| В1-2 | П2 унитаз подвесной | ½" | 250* | ст. Б: 446 от В | в раме инсталляции |
| К1-2 | П2 унитаз подвесной | Ø110 | 220* | ст. Б: 596 от В | |
| В1-3 | П3 умывальник | ½" | 600* | ст. Г: 546 от В | межос. 100 |
| Т3-2 | П3 умывальник | ½" | 600* | ст. Г: 446 от В | межос. 100 |
| К1-3 | П3 умывальник | Ø50 | 500* | ст. Г: 496 от В | |
| В1-4 | П4* стиральная машина | ½" | 600* | ст. Б: 586 от А | кран машины |
| К1-4 | П4* стиральная машина | Ø50 | 600* | ст. Б: 786 от А | |
| В1-5 | П11* мойка кухонная | ½" | 600 | ст. В: 935 от Г | межос. 100 |
| Т3-3 | П11* мойка кухонная | ½" | 600 | ст. В: 1035 от Г | межос. 100 |
| К1-5 | П11* мойка кухонная | Ø50 | 400 | ст. В: 985 от Г | |
| В1-6 | П12* посудомоечная машина | ½" | 550 | ст. В: 1285 от Г | кран ПММ в шкафу мойки |
| К1-6 | П12* посудомоечная машина | Ø40 | 550 | ст. В: 1185 от Г | слив ПММ в шкафу мойки |
| В1-7 | П6 душ | ½" | 1200* | ст. А: 451 от Г | межос. 150 |
| Т3-4 | П6 душ | ½" | 1200* | ст. А: 301 от Г | межос. 150 |
| К1-7 | П6 душ | Ø50 | 70* | ст. А: 376 от Г | сифон поддона |
| В1-8 | П7 унитаз подвесной | ½" | 250* | ст. В: 226 от Г | в раме инсталляции |
| К1-8 | П7 унитаз подвесной | Ø110 | 220* | ст. В: 376 от Г | |
| В1-9 | П8 умывальник | ½" | 600* | ст. Б: 326 от В | межос. 100 |
| Т3-5 | П8 умывальник | ½" | 600* | ст. Б: 426 от В | межос. 100 |
| К1-9 | П8 умывальник | Ø50 | 500* | ст. Б: 376 от В | |

* — высота по практике монтажа; сверить по паспорту прибора

### Условные обозначения

- вывод В1 (код — в ведомости привязок)
- вывод Т3 (код — в ведомости привязок)
- вывод К1 (код — в ведомости привязок)
- сантехприбор по расстановке (габарит модели)
- чистовая поверхность стены (от неё привязки)
- стояк «Ст К1-N / Ст В1-N» (ГОСТ 21.601), Ø мм
- * стояк Т3 не на обмере — принят в шахте рядом со Ст В1, сверить
- шахта / короб стояков, люк 300×400
- * у стояка — положение принято, не замерено, сверить
- линия обрыва (граница фрагмента)
- А обозначение стены А–Г (как на развёртках)

### Примечания

1. Привязки выводов даны от чистовых поверхностей стен (облицовка на сторону: ванная — 24 мм (штукатурка 10 + клей 5 + плитка 9); кухня-гостиная — 24 мм (фартук: штукатурка 10 + клей 5 + плитка 9); санузел 2 — 24 мм (штукатурка 10 + клей 5 + плитка 9)); эти же грани — на развёртках и в раскладке плитки. Высоты — от чистого пола помещения.
2. Высоты и межосевые, отмеченные «*», приняты по практике монтажа; до черновой разводки сверить по паспорту выбранного прибора (смеситель, инсталляция, сифон).
3. Горячая вода (Т3) — слева от холодной (В1), если смотреть на прибор. Допуск установки выводов: ±5 мм в группе, ±20 мм у отдельно стоящих.
4. Расчёт систем водоснабжения и канализации и подбор оборудования выполняет проектная организация; лист задаёт места и высоты выводов.
5. Посудомоечная машина П12*: кран и слив — отдельными выводами в шкафу мойки (не за машиной), до машины ≤ 1500 мм.
6. Ст Т3-1, Ст Т3-2 на обмере не показаны: приняты рядом с Ст В1-1*, Ст В1-2* (в МКД стоят группой); положение сверить на объекте до разметки.
7. Стояки в коробах/шахтах Ш1, Ш2 не замоноличивать; стояк К1 в коробе — звукоизоляция стояка в коробе без жёсткого контакта с трубой; к арматуре и ревизиям — люк не меньше 300×400.
8. Допущение проекта: санузел 2 — проектное решение: ниша 1600 × 1840 у входа (на плане открыта в кухню-гостиную) закрыта перегородкой по линии низа прихожей; ниша 660 × 260 у наружной стены (уступ по плану) закрыта фальш-стеной по линии уступа, в ней рама инсталляции унитаза.
9. Допущение проекта: стояки: у ванной — в коробе Ш1 248 × 459; у санузла 2 — в стене-пилоне 270 мм (Ш2) между санузлом 2 и кухней; люки 300 × 400; положение стояков условно — сверить на объекте.
10. Допущение проекта: кухня: раскладка гарнитура принята проектной, решение автора (ИЗ-12) — мойка М7* у шахты Ш2, ПММ М14* рядом с мойкой, варочная и духовой шкаф в М8*, вытяжка М15**, холодильник М6**; выводы техники — по типовой расстановке; условие: до начала черновых работ сверить раскладку и выводы с чертежом кухни от изготовителя, выводы пересматриваются по его чертежу (вопрос К-8).
11. Допущение проекта: стиральная машина П4* — вертикальной загрузки, габарит в плане 400 × 600 мм (ширина 400 вдоль стены Б): условие закупки, а не пожелание, решение автора (ИЗ-11); машина с фронтальной загрузкой или большего габарита не подходит — перед люком ванна П1; модель не выбрана, габарит и подводку сверить по паспорту до закрытия трасс (вопрос К-19).
12. Марки из допущений, которых нет на этом листе: М6**, М7*, М8*, М14*, М15** — лист 59.
13. Знак «*» у стояка — положение принято, не замерено (все стояки); сверить на объекте до разметки. Реестр: листы 6–11, вопрос К-17.

1000 мм · печать 1:1

| Изм. | Кол.уч | Лист | № док. | Подп. | Дата |
|---|---|---|---|---|---|
| Разраб. | | Кырлан А.С. | | | 05.10.26 |
| Пров. | | | | | |
| ГИП | | | | | |
| | | | | | |
| Н. контр. | | | | | |
| Утв. | | | | | |

**ГД-2026-003-АИ**

Трёхкомнатная квартира

Общая площадь 78,95* м² · * размеры со скана, не замерены (реестр — л. 6–11, К-13)

| Дизайн-проект интерьера трёхкомнатной квартиры | Стадия | Лист | Листов |
|---|---|---|---|
| | РП | 39 | 94 |

**План выводов сантехники**

М 1:50

Кырлан Александр Сергеевич

выпуск 05.10.2026 · 6add39ab8d · стр. 46 из 137

# Схема разводки водопровода и канализации

Схемы систем В1, Т3, К1 · трассы принципиальные · уклоны в мм на 1 м · план М 1:200, фрагменты М 1:40

## План квартиры (М 1:200)

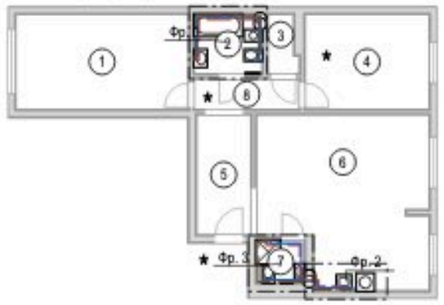


## Узел ввода В1, Т3 (схема, без масштаба)

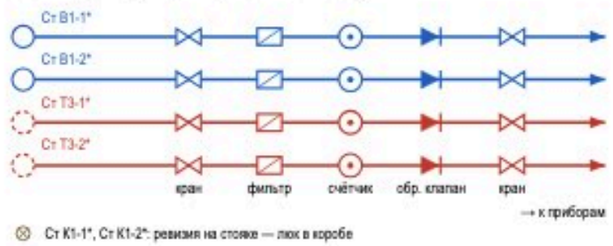


## Фр. 1. Ванная (М 1:40)

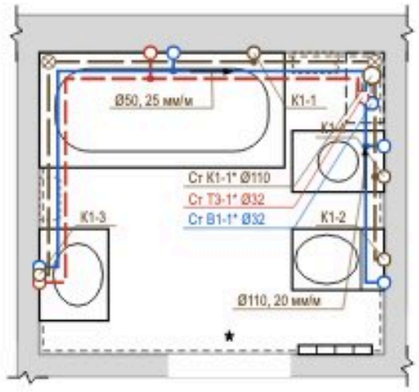


## Фр. 2. Кухня-гостиная (М 1:40)

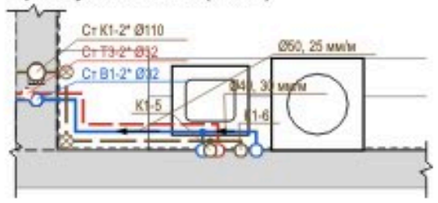


## Фр. 3. Санузел 2 (М 1:40)

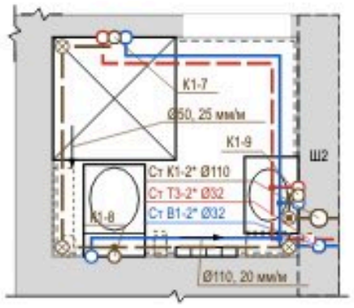


## Условные обозначения

- В1 — водопровод хозяйственно-питьевой (ХВС), PP-R Ø20
- Т3 — горячее водоснабжение, подача (ГВС), PP-R Ø20
- К1 — канализация бытовая
- направление уклона К1 / пола: Ø, мм на 1 м
- ⊗ ревизия (прочистка) К1 — доступ сохранить
- • тройник (ответвление к прибору)
- короб К1 над чистым полом (ГКЛВ под плитку)
- ○ вывод В1 (код — в ведомости привязок)
- ○ вывод Т3 (код — в ведомости привязок)
- ○ вывод К1 (код — в ведомости привязок)
- сантехприбор по расстановке (габарит модели)
- ○ стояк «Ст К1-N / Ст В1-N» (ГОСТ 21.601), Ø мм
- * стояк Т3 не на обмере — принят в шахте рядом со Ст В1, сверить
- ★ у стояка — положение принято, не замерено, сверить
- шахта / короб стояков, люк 300×400
- линия обрыва (граница фрагмента)
- граница фрагмента на плане (Фр. N)

## Профиль выпусков К1 (до врезки в стояк)

| Выпуск | Прибор | Ø | L, м | i, мм/м | Δh, мм | Прокладка, мм |
|---|---|---|---|---|---|---|
| К1-8 | П7 унитаз подвесной | Ø110 | 1,58 | 20 | 32 | короб 180×140 |
| К1-2 | П2 унитаз подвесной | Ø110 | 1,28 | 20 | 26 | над полом за приборами |
| К1-3 | П3 умывальник | Ø50 | 3,69 | 25 | 92 | короб 180×110 |
| К1-7 | П6 душ | Ø50 | 3,58 | 25 | 89 | короб 170×110 |
| К1-5 | П11* мойка кухонная | Ø50 | 1,65 | 25 | 41 | над полом за приборами |
| К1-1 | П1 ванна | Ø50 | 0,96 | 25 | 24 | короб 110×110 |
| К1-4 | П4* стиральная машина | Ø50 | 0,74 | 25 | 19 | над полом за приборами |
| К1-9 | П8 умывальник | Ø50 | 0,41 | 25 | 10 | над полом за приборами |
| К1-6 | П12* посудомоечная машина | Ø40 | 1,84 | 30 | 55 | над полом за приборами |

Короб h×b: h — от чистого пола, b — от чистовой стены. Стяжка 35 мм — лист полов.

## Примечания

1. Трассы принципиальные, построены от стояков вдоль стен помещений; фактическое положение фиксируется исполнительной схемой с привязками (фото с рулеткой) до закрытия.
2. Уклон К1 не менее 1/d и не более 150 мм/м (СП 30.13330.2020, п. 19.1), приняты практические уклоны; поворот — двумя отводами 45°, ревизия после поворота, доступ сохранить. Стояк К1 в коробе — звукоизоляция стояка в коробе, без жёсткого контакта короба с трубой.
3. Решение по К1: стяжка 35 мм не укрывает трубы (нужно Ø + Δh + 45 мм) — выпуски идут над чистым полом вдоль стен: К1-2, К1-5, К1-4, К1-9, К1-6 — за приборами и в раме инсталляции; К1-8, К1-3, К1-7, К1-1 — в коробе ГКЛВ под плитку (размеры в профиле). Короба — на развёртках; отметку низа врезки в стояк замерить до черновых работ.
4. На каждом вводе В1 и Т3 — кран шаровой, фильтр, счётчик, обратный клапан; доступ через люк не меньше 300×400. Водопровод — в штробе стен или в коробах; трубы испытать давлением до закрытия (акт скрытых работ).
5. Расчёт систем, диаметры магистралей и подбор оборудования выполняет проектная организация; врезка и перенос стояков — по согласованию с управляющей организацией. Арматуру и привязки сверить по паспортам приборов.
6. Ст Т3-1, Ст Т3-2 на обмере не показаны: приняты рядом с Ст В1-1*, Ст В1-2*; положение сверить на объекте до разводки.
7. Допущение проекта: санузел 2 — проектное решение: ниша 1600 × 1840 у входа (на плане открыта в кухню-гостиную) закрыта перегородкой по линии низа прихожей; ниша 660 × 260 у наружной стены (уступ по плану) закрыта фальш-стенкой по линии уступа, в ней рама инсталляции унитаза.
8. Допущение проекта: стояки: у ванной — в коробе Ш1 248 × 459; у санузла 2 — в стене-пилоне 270 мм (Ш2) между санузлом 2 и кухней; люки 300 × 400; положение стояков условно — сверить на объекте.
9. Допущение проекта: кухня: раскладка гарнитура принята проектной, решение автора (ИЗ-12) — мойка М7* у шахты Ш2, ПММ М14* рядом с мойкой, варочная и духовой шкаф в М8*, вытяжка М15**, холодильник М6**; выводы техники — по типовой расстановке; условие: до начала черновых работ сверить раскладку и выводы с чертежом кухни от изготовителя, выводы пересматриваются по его чертежу (вопрос К-8).
10. Допущение проекта: стиральная машина П4* — вертикальной загрузки, габарит в плане 400 × 600 мм (ширина 400 вдоль стены Б): условие закупки, а не пожелание, решение автора (ИЗ-11); машина с фронтальной загрузкой или большего габарита не подходит — перед люком ванна П1; модель не выбрана, габарит и подводку сверить по паспорту до закрытия трасс (вопрос К-19).
11. Марки из допущений, которых нет на этом листе: М6**, М7*, М8*, М14*, М15** — лист 59.
12. Знак «*» у стояка — положение принято, не замерено (все стояки); сверить на объекте до разметки. Реестр: листы 6–11, вопрос К-17.

Допущения и предложения на листе. Основа листа: размеры сняты со скана плана заказчика по размерным цепочкам, контрольный обмер на объекте не выполнялся (К-13); высота потолка 2700 мм принята: на плане заказчика не указана (К-11); толщины стен приняты: наружные 250 мм, перегородки 150 мм (на плане 85–190 мм) (К-13); разрешённая мощность 15 кВт принята по типовой квартире, технических условий нет (К-14); утолщение стены 190 × 1360 мм и элемент 1470 × 160 мм плана заказчика не определены (К-12); ниши санузла 2 закрыты перегородкой и фальш-стенкой: проектное решение, на плане заказчика ниша у входа открыта (К-18); несущие стены не определены: до технического заключения все существующие стены считаются несущими (К-20); окна существующие и сохраняются; подоконная доска и глубина откосов не заданы — приняты, не замерены (К-27). Знак «*» — принято, не замерено и не подтверждено (замерить на объекте): ИЗ-11, К-19: П4 — вертикальная загрузка 400 × 600 мм — условие закупки (решение автора, ИЗ-11); модель не выбрана, габарит сверить по паспорту. Знак «**» — предложение проектировщика, заказчиком не утверждено (согласовать с заказчиком). См. лист открытых вопросов (лист 6, записи К-8, К-11; лист 7, записи К-12–К-14, К-17–К-20; лист 8, записи К-25–К-27; лист 9, запись ИЗ-5; лист 10, записи ИЗ-11, ИЗ-16); по листу — К-17, ИЗ-16.

| | | | | | |
|---|---|---|---|---|---|
| | | | | | |
| | | | | | |
| | | | | | |
| Изм. | Кол.уч | Лист | № док. | Подп. | Дата |
| Разраб. | | Кырпан А.С. | | | 05.10.26 |
| Пров. | | | | | |
| ГИП | | | | | |
| | | | | | |
| Н. контр. | | | | | |
| Утв. | | | | | |

**ГД-2026-003-АИ**

Трёхкомнатная квартира

Общая площадь 78,95* м² · * размеры со скана, не замерены (реестр — п. 6–11, К-13)

| Дизайн-проект интерьера трёхкомнатной квартиры | Стадия | Лист | Листов |
|---|---|---|---|
| | РП | 40 | 94 |

**Схема разводки водопровода и канализации**

М 6/м

**Кырпан Александр Сергеевич**

выпуск 05.10.2026 № 6add39ab8d · стр. 47 из 137

# Спецификация сантехнического оборудования

Форма 1 ГОСТ 21.110-2013 · ГД-2026-003-АИ-ВК.СО · приборы, арматура, трубопроводы

**ПРЕДВАРИТЕЛЬНО · не для производства работ · открыто пунктов: 31 (реестр — л. 6–11)**

| Поз. | Наименование и техническая характеристика | Тип, марка, обозначение документа | Код продукции | Поставщик | Ед. изм. | Кол. | Масса 1 ед., кг | Примечание |
|---|---|---|---|---|---|---|---|---|
| | Санитарные приборы | | | | | | | |
| 1 | Ванна акриловая 1600×750 мм, с каркасом, экраном и отверстием слив-перелив | аналог | | выбор заказчика | шт | 1 | | П1 |
| 2 | Унитаз подвесной безободковый, с сиденьем микролифт, крепёж и звукоизолирующая прокладка | аналог | | выбор заказчика | шт | 2 | | П2, П7 |
| 3 | Инсталляция для подвесного унитаза: рама высотой 1120 мм, бачок, клавиша смыва (ось клавиши 1050 мм от чистого пола) | аналог | | выбор заказчика | шт | 2 | | П2, П7; короб ГКЛВ |
| 4 | Умывальник подвесной 450×600 мм, с отверстием под смеситель и переливом | аналог | | выбор заказчика | шт | 1 | | П3 |
| 5 | Умывальник подвесной 350×500 мм, с отверстием под смеситель и переливом | аналог | | выбор заказчика | шт | 1 | | П8 |
| 6 | Поддон душевой низкий 800×800 мм, с сифоном и выпуском Ø50, на ножках/подиуме | аналог | | выбор заказчика | шт | 1 | | П6 |
| 7 | Мойка кухонная врезная 500×450 мм, с переливом | аналог | | с кухонной мебелью | шт | 1 | | П11* |
| 8 | Полотенцесушитель электрический, IP44, с терморегулятором | аналог | | выбор заказчика | шт | 2 | | П10**, П12** |
| | Смесители, сифоны и арматура приборов | | | | | | | |
| 9 | Смеситель для ванны настенный однорычажный, межосевое 150 мм, с душевым набором (лейка, штанг, держатель) | аналог | | выбор заказчика | шт | 1 | | П1 |
| 10 | Смеситель для умывальника однорычажный, с донным клапаном | аналог | | выбор заказчика | шт | 2 | | П3, П8 |
| 11 | Душевая система скрытого монтажа с термостатом: встраиваемая часть, верхний душ, ручная лейка | аналог | | выбор заказчика | шт | 1 | | П6; встраиваемая часть — до плитки |
| 12 | Смеситель кухонный однорычажный, высокий излив | аналог | | выбор заказчика | шт | 1 | | П11* |
| 13 | Обвязка ванны слив-перелив Ø40/50 с сифоном | аналог | | выбор заказчика | шт | 1 | | П1 |
| 14 | Сифон для умывальника бутылочный Ø32/40–50, с гофрой к выпуску | аналог | | выбор заказчика | шт | 2 | | П3, П8 |
| 15 | Сифон для мойки с отводом для ПММ Ø40/50 | аналог | | выбор заказчика | шт | 1 | | П11* |
| 16 | Сифон для стиральной машины встраиваемый в стену Ø50, с обратным клапаном | аналог | | выбор заказчика | шт | 1 | | П4* |
| 17 | Кран угловой ½"×½" с гибкой подводкой 40 см (умывальники, мойка) | аналог | | выбор заказчика | шт | 6 | | по 2 на прибор |
| 18 | Кран шаровой угловой ½"×¾" для подключения стиральной и посудомоечной машины | аналог | | выбор заказчика | шт | 2 | | П4*, П12* |
| | Трубопроводы | | | | | | | |
| 19 | Труба полипропиленовая PP-R PN20 Ø20×3,4 (В1) | ГОСТ 32415-2013 | | выбор заказчика | м | 18,5 | 0,17 | 11,2 + 5,5 + 10 % |
| 20 | Труба PP-R, армированная стекловолокном, PN20 Ø20×2,8 (Т3) | ГОСТ 32415-2013 | | выбор заказчика | м | 13,5 | 0,15 | 8,2 + 3,8 + 10 % |
| 21 | Труба канализационная ПП Ø40 (К1) | ГОСТ 32414-2013 | | выбор заказчика | м | 1 | | 0,3 + 0,6 + 10 % |
| 22 | Труба канализационная ПП Ø50 (К1) | ГОСТ 32414-2013 | | выбор заказчика | м | 11 | | 7,7 + 2,1 + 10 % |
| 23 | Труба канализационная ПП Ø110 (К1) | ГОСТ 32414-2013 | | выбор заказчика | м | 4 | | 2,9 + 0,4 + 10 % |
| | Фасонные части и выводы | | | | | | | |
| 24 | Отвод канализационный ПП 45° Ø40 | ГОСТ 32414-2013 | | выбор заказчика | шт | 2 | | 2 шт. на поворот |
| 25 | Отвод канализационный ПП 45° Ø50 | ГОСТ 32414-2013 | | выбор заказчика | шт | 20 | | 2 шт. на поворот |
| 26 | Отвод канализационный ПП 45° Ø110 | ГОСТ 32414-2013 | | выбор заказчика | шт | 10 | | 2 шт. на поворот |
| 27 | Тройник канализационный ПП 45° (врезки ветвей) | ГОСТ 32414-2013 | | выбор заказчика | шт | 8 | | |
| 28 | Ревизия канализационная ПП (после поворота трассы) | ГОСТ 32414-2013 | | выбор заказчика | шт | 9 | | доступ сохранить |
| 29 | Фитинги PP-R Ø20: тройники, угольники 90° (ветви и повороты В1, Т3) | ГОСТ 32415-2013 | | выбор заказчика | шт | 34 | | |
| 30 | Водорозетка PP-R Ø20×½" настенная, с креплением | ГОСТ 32415-2013 | | выбор заказчика | шт | 14 | | коды — лист выводов |
| | Узлы ввода, люки, короба | | | | | | | |
| 31 | Кран шаровой латунный Ду15 PN16 (отключение ввода) | аналог | | выбор заказчика | шт | 4 | | Ст В1-1*, Ст В1-2*, Ст Т3-1*, Ст Т3-2* |
| 32 | Фильтр сетчатый косой Ду15 | аналог | | выбор заказчика | шт | 4 | | |
| 33 | Счётчик воды крыльчатый Ду15 (ХВ, ГВ), с поверкой | аналог | | выбор заказчика | шт | 4 | | пломба УК |
| 34 | Клапан обратный Ду15 | аналог | | выбор заказчика | шт | 4 | | |
| 35 | Люк ревизионный накимной под плитку 300×400 мм | аналог | | выбор заказчика | шт | 2 | | к стоякам и арматуре |
| 36 | Звукоизоляция стояка К1 в коробе: рулонный звукоизоляционный материал ≥ 10 мм, обмотка стояка на высоту этажа | аналог | | выбор заказчика | м | 5,4 | | Ст К1-1*, Ст К1-2* |
| 37 | Короб К1 над полом: профиль ПНПС, ГКЛВ 12,5 мм под плитку | аналог | | выбор заказчика | м | 2,4 | | сечение — лист разводки |

## Примечания

1. Форма 1 ГОСТ 21.110-2013, ширины граф изменены по п. 4.1. «Аналог» — аналог по характеристикам: модели внести до черновых работ, привязки выводов сверить по паспортам.
2. Бытовая техника не входит (показана арматура подключения), мойка — в комплекте кухни. Длины труб — трасса листа разводки + подъёмы + 10 %.
3. Стояк К1 в коробе — звукоизоляция стояка в коробе без жёсткого контакта короба с трубой. Стояки со «*» (Ст К1-1*, Ст В1-1*, Ст К1-2*, Ст В1-2*, Ст Т3-1, Ст Т3-2) приняты — положение и число узлов ввода сверить на объекте.
4. Расчёт систем водоснабжения и канализации, диаметры магистралей и подбор оборудования выполняет проектная организация.
5. Допущение проекта: санузел 2 — проектное решение: ниша 1600 × 1840 у входа (на плане открыта в кухню-гостиную) закрыта перегородкой по линии низа прихожей; ниша 660 × 260 у наружной стены (уступ по плану) закрыта фальш-стеной по линии уступа, в ней рама инсталляции унитаза.
6. Допущение проекта: стояки: у ванной — в коробе Ш1 248 × 459; у санузла 2 — в стене-пилоне 270 мм (Ш2) между санузлом 2 и кухней; люки 300 × 400; положение стояков условно — сверить на объекте.
7. Допущение проекта: кухня: раскладка гарнитура принята проектной, решение автора (ИЗ-12) — мойка М7* у шахты Ш2, ПММ М14* рядом с мойкой, варочная и духовой шкаф в М8*, вытяжка М15**, холодильник М6**; выводы техники — по типовой расстановке; условия: до начала черновых работ сверить раскладку и выводы с чертежом кухни от изготовителя, выводы пересматриваются по его чертежу (вопрос К-8).
8. Допущение проекта: стиральная машина П4* — вертикальной загрузки, габарит в плане 400 × 600 мм (ширина 400 вдоль стены Б): условие закупки, а не пожелание, решение автора (ИЗ-11); машина с фронтальной загрузкой или большего габарита не подходит — перед люком ванна П1; модель не выбрана, габарит и подводку сверить по паспорту до закрытия трасс (вопрос К-19).
9. Марки из допущений, которых нет на этом листе: М6**, М7*, М8*, М14*, М15** — лист 59.

**Допущения и предложения на листе**

Основа листа: размеры сняты со скана плана заказчика по размерным цепочкам, контрольный обмер на объекте не выполнялся (К-13); высота потолка 2700 мм принята: на плане заказчика не указана (К-11); толщины стен приняты: наружные 250 мм, перегородки 150 мм (на плане 85–190 мм) (К-13); разрешённая мощность 15 кВт принята по типовой квартире, технических условий нет (К-14); утолщение стены 190 × 1360 мм и элемент 1470 × 160 мм плана заказчика не определены (К-12); ниши санузла 2 закрыты перегородкой и фальш-стеной: проектное решение, на плане заказчика ниша у входа открыта (К-18); несущие стены не определены: до технического заключения все существующие стены считаются несущими (К-20); окна существующие и сохраняются; подоконная доска и глубина откосов не заданы — приняты, не замерены (К-27).

Знак «*» — принято, не замерено и не подтверждено (замерить на объекте): ИЗ-11, К-19: П4 — вертикальная загрузка 400 × 600 мм — условие закупки (решение автора, ИЗ-11); модель не выбрана, габарит сверить по паспорту; К-8: М7, М14, М8, П11, П12; К-17: Ст К1-1, Ст В1-1, Ст К1-2, Ст В1-2.

Знак «**» — предложение проектировщика, заказчиком не утверждено (согласовать с заказчиком): ИЗ-1: П10, П13; ИЗ-5, К-8: М6, М15.

Открытые вопросы и конфликты по листу: К-19.

Изменения по листу без подписи: ИЗ-16.

См. лист открытых вопросов (лист 6, записи К-8, К-11; лист 7, записи К-12–К-14, К-17–К-20; лист 8, запись К-27; лист 9, записи ИЗ-1, ИЗ-5; лист 10, записи ИЗ-11, ИЗ-16).

| | | | | | |
|---|---|---|---|---|---|
| | | | | | |
| | | | | | |
| | | | | | |
| Изм. | Кол.уч | Лист | № док. | Подп. | Дата |
| Разраб. | | Кырлан А.С. | | | 05.10.26 |
| Пров. | | | | | |
| ГИП | | | | | |
| | | | | | |
| Н. контр. | | | | | |
| Утв. | | | | | |

**ГД-2026-003-АИ**

Трёхкомнатная квартира

Общая площадь 78,95* м² · * размеры со скана, не замерены (реестр — л. 6–11, К-13)

Дизайн-проект интерьера трёхкомнатной квартиры

| Стадия | Лист | Листов |
|---|---|---|
| РП | 41 | 94 |

Спецификация сантехнического оборудования

М 6/м

Кырлан Александр Сергеевич

выпуск 05.10.2026 · 6add39ab8d · стр. 48 из 137

# Спецификация светильников и сценарии освещения

Светильники, ленты и блоки питания, слои света и сценарии по помещениям · б/м

## Спецификация светильников

| Поз. | Марки | Наименование | Установка | Кол. | P, Вт | Σ P, Вт | Ф, лм | Tц, K | Ra | Угол, ° | IP | Дим. | Группа | Пом. |
|---|---|---|---|---|---|---|---|---|---|---|---|---|---|---|
| 1 | Св1–Св8 | Встраиваемый точечный | в ГКЛ, корпус ≤ 70 мм | 8 | 12 | 96 | 1000 | 2700 | 90 | — | 20 | — | L1 | 1 |
| 2 | Св9 | Лента светодиодная 24 В | в карнизе короба, профиль с рассеивателем | 15,5 м | 9,6/м | 148,8 | 900/м | 2700 | 90 | — | 20 | да | L2 | 1 |
| 3 | Св10, Св11, Св24, Св25 | Настенный (бра) | на стене, H=1500 | 4 | 6 | 24 | 400 | 2700 | 90 | 60 | 20 | — | L3, L9 | 1, 4 |
| 4 | Св12–Св14, Св51 | Встраиваемый точечный | в ГКЛ, корпус ≤ 70 мм | 4 | 6 | 24 | 500 | 3000 | 90 | — | 44 | — | L4, L17 | 2, 7 |
| 5 | Св15, Св52 | Настенный светильник над зеркалом, драйвер встроен | над зеркалом, H=1900 | 2 | 8 | 16 | 600 | 3000 | 90 | — | 44 | — | L5, L18 | 2, 7 |
| 6 | Св16 | Потолочный накладной | на потолке, засветка стены | 1 | 10 | 10 | 900 | 3000 | 90 | — | 20 | — | L6 | 3 |
| 7 | Св17–Св22 | Встраиваемый точечный | в ГКЛ, корпус ≤ 70 мм | 6 | 12 | 72 | 1050 | 2700 | 90 | — | 20 | — | L7 | 4 |
| 8 | Св23 | Лента светодиодная 24 В | в карнизе короба, профиль с рассеивателем | 12,3 м | 9,6/м | 118,5 | 900/м | 2700 | 90 | — | 20 | да | L8 | 4 |
| 9 | Св26–Св29, Св53, Св54 | Встраиваемый точечный | в ГКЛ, корпус ≤ 70 мм | 6 | 7 | 42 | 600 | 3000 | 90 | — | 20 | — | L10 | 5, 8 |
| 10 | Св30 | Лента светодиодная 24 В | в коробе, профиль с рассеивателем, датчик движения | 1,8 м | 4,8/м | 8,6 | 150/м | 2700 | 90 | — | 20 | нет | L11 | 6 |
| 11 | Св31–Св40 | Встраиваемый точечный | в ГКЛ, корпус ≤ 70 мм | 10 | 12 | 120 | 1000 | 3000 | 90 | — | 20 | да | L12 | 6 |
| 12 | Св41 | Лента светодиодная 24 В | в карнизе короба, профиль с рассеивателем | 22,1 м | 9,6/м | 211,8 | 900/м | 2700 | 90 | — | 20 | да | L13 | 6 |
| 13 | Св42**, Св43**, Св44** | Подвесной | подвес, низ H=1450 | 3 | 9 | 27 | 800 | 3000 | 90 | — | 20 | да | L14 | 6 |
| 14 | Св45–Св48 | Встраиваемый точечный | в ГКЛ, корпус ≤ 70 мм | 4 | 10 | 40 | 900 | 3000 | 90 | — | 20 | да | L15 | 6 |
| 15 | Св49** | Линейный настенный | под верхними шкафами, H=1440 | 1 | 18 | 18 | 1500 | 3000 | 90 | — | 20 | да | L16 | 6 |
| 16 | Св50 | Встраиваемый точечный | в ГКЛ, корпус ≤ 70 мм | 1 | 7 | 7 | 600 | 3000 | 90 | — | 44 | — | L17 | 7 |
| | | **Итого** | | **50 шт + 51,7 м** | | **983,7** | | | | | | | | |

## Слои света по помещениям

| Пом. | Помещение | Слои света и группы включения (марки светильников) | Tц, K | Ra | Σ P, Вт | Сцен. |
|---|---|---|---|---|---|---|
| 1 | Спальня 1 | общий — L1 (Св1–Св8); рабочий — L3 (Св10, Св11); акцентный — L2 (Св9) | 2700 | 90 | 256,8 | 2 |
| 2 | Ванная | общий — L4 (Св12–Св14); рабочий — L5 (Св15) | 3000 | 90 | 26 | — |
| 3 | Гардеробная | общий — L6 (Св16) | 3000 | 90 | 10 | — |
| 4 | Спальня 2 | общий — L7 (Св17–Св22); рабочий — L9 (Св24, Св25); акцентный — L8 (Св23) | 2700 | 90 | 202,5 | 1 |
| 5 | Прихожая | общий — L10 (Св26–Св29); ночной — L11 (Св30) | 2700 / 3000 | 90 | 36,6 | — |
| 6 | Кухня-гостиная | общий — L12 (Св31–Св40), L14 (Св42**, Св43**, Св44**), L15 (Св45–Св48); рабочий — L16 (Св49**); акцентный — L13 (Св41) | 2700 / 3000 | 90 | 416,8 | 4 |
| 7 | Санузел 2 | общий — L17 (Св50, Св51); рабочий — L18 (Св52) | 3000 | 90 | 21 | — |
| 8 | Коридор | общий — L10 (Св53, Св54) | 3000 | 90 | 14 | — |

## Примечания

1. Позиции и марки Св — те же, что на плане освещения (лист 30) и в ведомости светильников (лист 32); группы L — по плану выключателей (лист 31).
2. Модели светильников не назначены: подбор по графам спецификации — поток, Tц, Ra, угол, IP и диммирование не хуже указанных, мощность не больше; встраиваемые — под глубину короба (графа «Установка»). IP 20 — сухие помещения.
3. Длина LED-ленты в карнизе — по линии карниза плана потолков (лист 44); Σ P = Вт/м × длина. Блок питания загружен не больше чем на 80 %; лента 24 В длиннее 10 м питается с двух концов; доступ к блоку питания — люк ревизии 300×300 мм или место, указанное в таблице.
4. Сценарии: уровень — доля максимальной яркости группы, %; 0 — группа выключена. Уровень ниже 100 % — только у групп на светорегуляторе (задний фронт, TE) с диммируемыми драйверами и блоками питания.
5. Мощность и поток — по паспортам принятых изделий, Σ P — установленная мощность освещения. Оценка освещённости — на плане освещения; это не светотехнический расчёт.

## LED-ленты, линейные светильники и блоки питания

| Марка | Пом. | L, м | U, В | Вт/м | Σ P, Вт | БП | P БП, Вт | Загр., % | Питание | Доступ к БП |
|---|---|---|---|---|---|---|---|---|---|---|
| Св9 | 1 | 15,5 | 24 | 9,6 | 148,8 | БП1 | 200 | 74 | с двух концов | люк 300×300 в коробе У1 у входа |
| Св23 | 4 | 12,3 | 24 | 9,6 | 118,5 | БП2 | 200 | 59 | с двух концов | люк 300×300 в коробе У1 у окна |
| Св30 | 5 | 1,8 | 24 | 4,8 | 8,6 | БП3 | 20 | 43 | с одного конца | в шкафу М16, верхняя полка |
| Св41 | 6 | 22,1 | 24 | 9,6 | 211,8 | БП4 | 300 | 71 | с двух концов | люк 300×300 в коробе У1 у входа |
| Св49** | 6 | 3 | 24 | — | 18 | БП5** | 60 | 30 | встроенный ввод | в пенале М6**, верх, съёмная панель |

## Сценарии освещения

| Пом. | Сценарий | Группы и уровни, % | Чем включается |
|---|---|---|---|
| 1 | Вечер | L1 споты — 0; L2 подсветка короба — 100; L3 бра — 100 | S1, S2, S3 |
| 1 | Уборка | L1 споты — 100; L2 подсветка короба — 100; L3 бра — 0 | S1, S2, S3 |
| 4 | Вечер | L7 споты — 0; L8 подсветка короба — 100; L9 бра — 100 | S4, S5, S6 |
| 6 | Вечер | L12 споты гостиной — 30; L13 подсветка короба — 100; L14 подвесы над столом — 50; L15 споты кухни — 0; L16 подсветка столешницы — 0 | S10 светорегулятор, S11** светорегулятор |
| 6 | Ужин | L12 споты гостиной — 0; L13 подсветка короба — 60; L14 подвесы над столом — 100; L15 споты кухни — 0; L16 подсветка столешницы — 30 | S10 светорегулятор, S11** светорегулятор, S12** светорегулятор |
| 6 | Кино | L12 споты гостиной — 0; L13 подсветка короба — 20; L14 подвесы над столом — 0; L15 споты кухни — 0; L16 подсветка столешницы — 0 | S10 светорегулятор |
| 6 | Готовка | L12 споты гостиной — 50; L13 подсветка короба — 0; L14 подвесы над столом — 0; L15 споты кухни — 100; L16 подсветка столешницы — 100 | S10 светорегулятор, S11** светорегулятор, S12** светорегулятор |
| все | Ушёл | все группы — 0 (свет выключен) | выключатели помещений |

## Слои света

общий — равномерный свет помещения, по норме освещённости

рабочий — местный свет задачи: столешница, зеркало, чтение у кровати

акцентный — подсветка потолка, стен и ниш; не входит в поток общего света

ночной — путь спальня → санузел: не выше 2700 K, малая яркость, датчик движения

Допущения и предложения на листе. Основа листа: размеры сняты со скана плана заказчика по размерным цепочкам, контрольный обмер на объекте не выполнялся (К-13); высота потолка 2700 мм принята: на плане заказчика не указана (К-11); толщины стен приняты: наружные 250 мм, перегородки 150 мм (на плане 85–190 мм) (К-13); разрешённая мощность 15 кВт принята по типовой квартире, технических условий нет (К-14); утолщение стены 190 × 1360 мм и элемент 1470 × 160 мм плана заказчика не определены (К-12); ниши санузла 2 закрыты перегородкой и фальш-стеной: проектное решение, на плане заказчика ниша у входа открыта (К-18); несущие стены не определены: до технического заключения все существующие стены считаются несущими (К-20); окна существующие и сохраняются; подоконная доска и глубина откосов не заданы — приняты, не замерены (К-27). Знак «**» — предложено, не утверждено (согласовать): ИЗ-3: S11, S12, Св42, Св43, Св44, Св49, БП5. См. лист открытых вопросов (лист 6, записи К-8, К-11; лист 7, записи К-12–К-14, К-18, К-20; лист 8, запись К-27; лист 9, записи ИЗ-3, ИЗ-5).

| Изм. | Кол.уч | Лист | № док. | Подп. | Дата |
|---|---|---|---|---|---|
| Разраб. | | Кырпан А.С. | | | 05.10.26 |
| Пров. | | | | | |
| ГИП | | | | | |
| | | | | | |
| Н. контр. | | | | | |
| Утв. | | | | | |

**ГД-2026-003-АИ**

Трёхкомнатная квартира

Общая площадь 78,95* м² · * размеры со скана, не замерены (реестр — п. 6–11, К-13)

Дизайн-проект интерьера трёхкомнатной квартиры

| Стадия | Лист | Листов |
|---|---|---|
| РП | 42 | 94 |

**Спецификация светильников и сценарии освещения**
М б/м

**Кырпан Александр Сергеевич**

выпуск 05.10.2026 № 6add39ab8d · стр. 49 из 137

# Схема каркаса перегородки П-1**

С112; вид, сечения и узлы: каркас, обрамление проёма и примыкания

## Вид на каркас без обшивки (М 1:20)

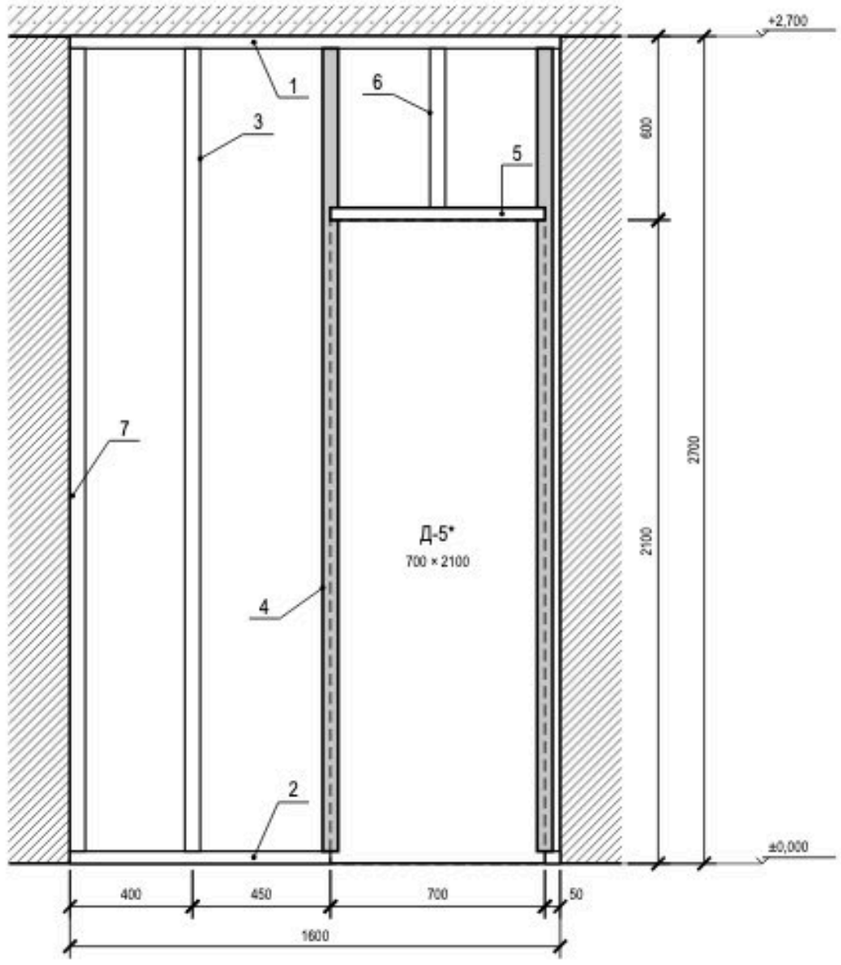


Оси — стойки каркаса; полки профиля на виде условны

## Сечение А–А по стойке (М 1:5)

сверху — пом. 6, окраска

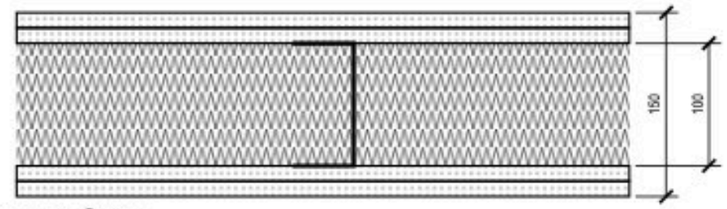


снизу — пом. 7, плитка

поз. 9 — ГКЛВ 12,5 мм в 2 слоя с каждой стороны; поз. 3 — ПС 100; поз. 8 — минвата 100 мм (принято)

## Сечение Б–Б у проёма, на уровне ниже перемычки (М 1:5)

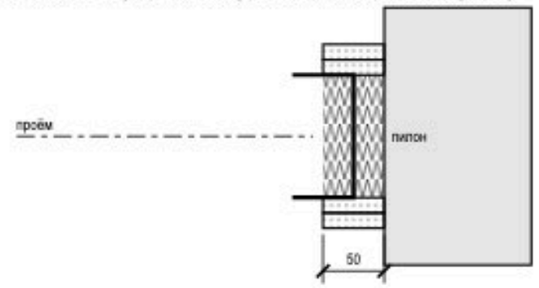


поз. 4 — УА 100, обрамление проёма; обшивка по краю проёма, простенок 50 мм до пилона

## Узел 1. К плите (М 1:5)

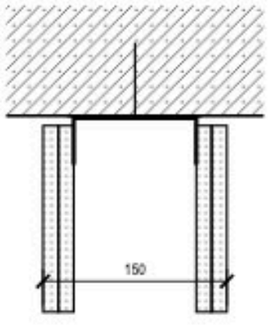


## Узел 2. К полу (М 1:5)

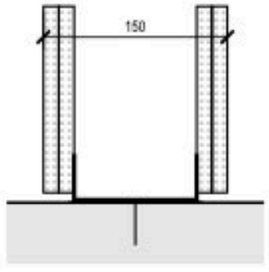


## Ведомость элементов каркаса

| Поз. | Наименование | Кол-во | Ед. |
|---|---|---|---|
| 1 | ПН 100 по потолку (по плите) | 1,60 | м |
| 2 | ПН 100 по полу, без проёма | 0,90 | м |
| 3 | ПС 100 через 400 мм | 2 × 2,70 | м |
| 4 | УА 100 по краям проёма | 2 × 2,70 | м |
| 5 | ПН 100 перемычка над проёмом | 0,70 | м |
| 6 | ПС 100 над перемычкой | 1 × 0,60 | м |
| 7 | Лента уплотнительная под профили | 7,90 | м |
| 8 | Минвата в полость, 100 мм | 2,85 | м² |
| 9 | ГКЛВ 12,5 мм, 2 слоя с двух сторон | 11,40 | м² |

Итого: ПН 3,20 м, ПС 6,00 м, УА 5,40 м; сторона 2,85 м²

## Примечания

1. П-1** (С112, ГКЛВ в 2 слоя с каждой стороны, толщина 150 мм, высота 2700 мм до плиты) — предложение проектировщика, автором не утверждено (К-18, К-4); ось и длина 1600 мм — со скана плана заказчика (контрольный обмер не выполнялся).
2. Шаг стоек 400 мм — по данным (под плитку и во влажной зоне). Размеры сечений профилей — «ПС 100», «УА 100» по данным и каталогу; толщины листов — ГОСТ 32614-2012.
3. Принято: стойка ПС на 800 мм не ставится: ось в 50 мм от УА на 850 мм, два профиля с полкой 50 мм не помещаются — УА проёма служит и стойкой каркаса; полка 50 мм принята по каталогу Knauf (К-18, К-4).
4. Принято: стойка ПС на 1600 мм не ставится: ось в 50 мм от УА на 1550 мм, два профиля с полкой 50 мм не помещаются — УА проёма служит и стойкой каркаса у конца перегородки; полка 50 мм принята по каталогу Knauf (К-18, К-4).
5. Принято: проём Д-5 в каркасе 700 × 2100 мм принят по размеру полотна: короб скрытой двери (модель, размеры) не выбран — проём пересчитать по коробке до монтажа УА (К-18, К-4).
6. Принято: перемычка над проёмом — направляющий профиль по верху проёма на всю его ширину; короткие стойки ПС над перемычкой на шаге каркаса: по практике узла Knauf, не по данным объекта (К-18, К-4).
7. Принято: заполнение полости — минераловатная плита на всю глубину профиля (Rw системы С112 нормируют с заполнением); марка и плотность выбираются при закупке (К-18, К-4).
8. Принято: длина стойки равна высоте перегородки: стойки режут на высоту между направляющими при монтаже, зазоры до плиты и пола в данных не заданы (edgeGaps).
9. Принято: простенок 50 мм между проёмом Д-5 и концом перегородки: УА проёма — последняя стойка в 50 мм от примыкания, полоса обшивки в 50 мм уже удобной ширины; решение по положению проёма — за автором (К-18, К-4).
10. Обшивку крепят к стойкам шурупами через слой, швы слоёв вразбежку; зазоры обшивки до плиты и пола, шаг дюбелей, марка заполнения — по ТУ системы и узлу изготовителя.

**Допущения и предложения на листе**

Основа листа: размеры сняты со скана плана заказчика по размерным цепочкам, контрольный обмер на объекте не выполнялся (К-13); высота потолка 2700 мм принята: на плане заказчика не указана (К-11); толщины стен приняты: наружные 250 мм, перегородки 150 мм (на плане 85–190 мм) (К-13); разрешённая мощность 15 кВт принята по типовой квартире, технических условий нет (К-14); утолщение стены 190 × 1360 мм и элемент 1470 × 160 мм плана заказчика не определены (К-12); ниши санузла 2 закрыты перегородкой и фальш-стеной: проектное решение, на плане заказчика ниша у входа открыта (К-18); несущие стены не определены: до технического заключения все существующие стены считаются несущими (К-20); окна существующие и сохраняются; подоконная доска и глубина откосов не заданы — приняты, не замерены (К-27).

Знак «**» — предложение проектировщика, заказчиком не утверждено (согласовать с заказчиком): К-4, К-18: П-1 — проектное решение исполнителя: на плане заказчика ниша у входа открыта в кухню-гостиную; конструкция не утверждена автором (вопрос К-18), положение и размеры сняты со скана (К-13).

См. лист открытых вопросов (лист 6, записи К-4, К-11; лист 7, записи К-12–К-14, К-18, К-20; лист 8, запись К-27).

| Изм. | Кол.уч | Лист | № док. | Подп. | Дата |
|---|---|---|---|---|---|
| Разраб. | | Кырлан А.С. | | | 05.10.26 |
| Пров. | | | | | |
| ГИП | | | | | |
| | | | | | |
| Н. контр. | | | | | |
| Утв. | | | | | |

**ГД-2026-003-АИ**

Трёхкомнатная квартира

Общая площадь 78,95* м² · * размеры со скана, не замерены (реестр — п. 6–11, К-13)

Дизайн-проект интерьера трёхкомнатной квартиры

| Стадия | Лист | Листов |
|---|---|---|
| РП | 43 | 94 |

**Схема каркаса перегородки П-1**

по видам

Кырлан Александр Сергеевич

выпуск 05.10.2026 · 6add39ab8d · стр. 50 из 137

06

# Потолки и ГКЛ-конструкции

Кырлан Александр Сергеевич

выпуск 05.10.2026 № 6add39ab8d - стр. 51 из 137

# План потолков

Уровни и марки потолков, короба с подсветкой, ниши под шторы, люки, вырезы · отметки низа от ±0,000 чистого пола · размеры в мм

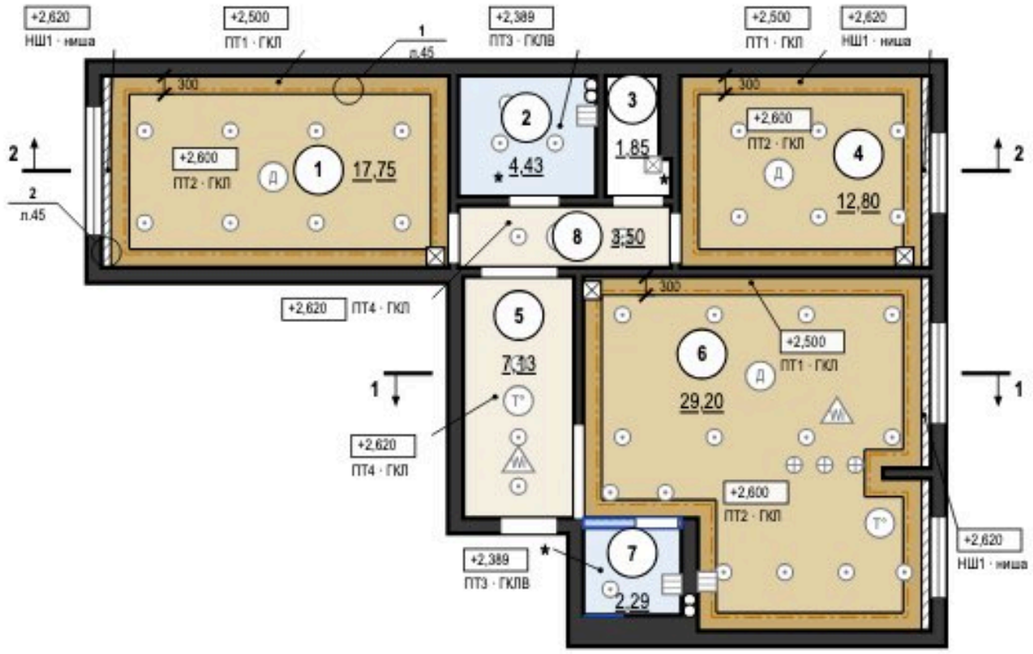


## Ведомость потолков

| Пом. | Марка | Конструкция | Низ | S, м² | Q |
|---|---|---|---|---|---|
| 1 | ПТ1 | ГКЛ П113, короб LED | +2,500 | 4,83 | Q3 |
| 1 | ПТ2 | ГКЛ П113 | +2,600 | 12,45 | Q3 |
| 1 | НШ1 | ниша под шторы 150×120 | +2,620 | 0,47 | |
| 2 | ПТ3 | ГКЛВ П113 | +2,389 | 4,43 | Q3 |
| 3 | | по плите, окраска | +2,700 | 1,85 | |
| 4 | ПТ1 | ГКЛ П113, короб LED | +2,500 | 3,88 | Q3 |
| 4 | ПТ2 | ГКЛ П113 | +2,600 | 8,45 | Q3 |
| 4 | НШ1 | ниша под шторы 150×120 | +2,620 | 0,47 | |
| 5 | ПТ4 | ГКЛ П113 | +2,620 | 7,13 | Q3 |
| 6 | ПТ1 | ГКЛ П113, короб LED | +2,500 | 6,80 | Q3 |
| 6 | ПТ2 | ГКЛ П113 | +2,600 | 21,56 | Q3 |
| 6 | НШ1 | ниша под шторы 150×120 | +2,620 | 0,84 | |
| 7 | ПТ3 | ГКЛВ П113 | +2,389 | 2,29 | Q3 |
| 8 | ПТ4 | ГКЛ П113 | +2,620 | 3,50 | Q3 |
| | | **Итого** | | **78,95** | |

## Ведомость вырезов и закладных в потолке

| Марка | Устройство | Кол. | Пом. |
|---|---|---|---|
| | Светильник встраиваемый (марки — план освещения) | 39 | 1, 2, 4, 5, 6, 7, 8 |
| | Светильник накладной (марки — план освещения) | 1 | 3 |
| | Светильник подвесной (марки — план освещения) | 3 | 6 |
| ИП1, ИП2, ИП4 | Извещатель дымовой | 3 | 1, 4, 6 |
| ИП3, ИП5, ИП6 | Извещатель тепловой | 3 | 5, 6, 8 |
| AP1**, AP2** | Точка доступа Wi-Fi, PoE | 2 | 5, 6 |
| ВР1…ВР3 | Решётка вытяжная (вентилятор) | 3 | 2, 6, 7 |
| | Люк ревизии 300×300 | 3 | 1, 4, 6 |

**Допущения и предложения на листе**

Основа листа: размеры сняты со скана плана заказчика по размерным цепочкам, контрольный обмер на объекте не выполнялся (К-13); высота потолка 2700 мм принята: на плане заказчика не указана (К-11); толщины стен приняты: наружные 250 мм, перегородки 150 мм (на плане 85–190 мм) (К-13); разрешённая мощность 15 кВт принята по типовой квартире, технических условий нет (К-14); утолщение стены 190 × 1360 мм и элемент 1470 × 160 мм плана заказчика не определены (К-12); ниши санузла 2 закрыты перегородкой и фальш-стеной: проектное решение, на плане заказчика ниша у входа открыта (К-18); несущие стены не определены: до технического заключения все существующие стены считаются несущими (К-20); окна существующие и сохраняются; подоконная доска и глубина откосов не заданы — приняты, не замерены (К-27).

Знак «*» — принято, не замерено и не подтверждено (замерить на объекте): К-17: Ст К1-1, Ст В1-1, Ст К1-2, Ст В1-2; К-25: дверь пом. 8 (стена А) — толщина стены в проёме принята 150 мм (как у всех перегородок модели), по скану плана заказчика стена 85 мм — не замерено (К-25); проём существующий, скрытый блок ставится в него с зазором 10–15 мм на сторону, полотно уже проёма; узел скрытой двери выполнен для принятой толщины 150 мм; К-26: дверь пом. 5 (стена В) — входная дверь существующая; по плану заказчика полотно открывается наружу, в общий коридор — направление взято с плана и на объекте не проверено; остаётся ли существующий блок или он заменяется — не решено (К-26).

Знак «**» — предложение проектировщика, заказчиком не утверждено (согласовать с заказчиком): ИЗ-17: AP1, AP2 — точка доступа Wi-Fi: число и места; К-4, К-18: П-1 — проектное решение исполнителя: на плане заказчика ниша у входа открыта в кухню-гостиную; конструкция не утверждена автором (вопрос К-18), положение и размеры сняты со скана (К-13); К-18: П-2 — проектное решение исполнителя: на плане заказчика у наружной стены уступ 660 × 260 мм; конструкция не утверждена автором (вопрос К-18).

См. лист открытых вопросов (лист 6, записи К-4, К-11; лист 7, записи К-12–К-14, К-17, К-18, К-20; лист 8, записи К-25–К-27; лист 11, запись ИЗ-17).

## Условные обозначения

- ПТ1 — ГКЛ по каркасу П113, низ +2,500, пояс-короб с карнизом LED
- ПТ2 — ГКЛ по каркасу П113, низ +2,600
- ПТ3 — ГКЛВ по каркасу П113, низ +2,389
- ПТ4 — ГКЛ по каркасу П113, низ +2,620
- потолок по плите перекрытия, окраска, низ +2,700
- НШ1 — ниша под шторы 150×120, верх +2,620
- граница уровней потолка (перепад)
- LED-лента в карнизе короба (подсветка верхнего уровня)
- люк ревизии в потолке 300×300 мм (доступ к БП LED)
- светильник встраиваемый — подложка с плана освещения
- светильник накладной — подложка с плана освещения
- светильник подвесной — подложка с плана освещения
- Д — извещатель дымовой на потолке — подложка
- Т° — извещатель тепловой на потолке — подложка
- Wi — точка доступа Wi-Fi на потолке — подложка
- решётка вытяжки в потолке — подложка с плана вентиляции
- линия разреза, стрелка — направление взгляда (разрезы — лист 45)
- место узла: номер узла на полке, под полкой — лист (узлы — лист 45)
- +2,6 — отметка низа потолка, м; под ней марка потолка
- новое — возводится по проекту (синим)
- 1 — номер помещения, площадь м²

## Примечания

1. За отметку ±0,000 принят уровень чистого пола сухих помещений (готовое покрытие), а не существующего пола; пол пом. 2, 7 — −0,015; верх плиты перекрытия −0,064 — расчётный по пирогу пола, не замерен; существующий пол снимается до плиты, его отметка не замерена. Отметки в прямоугольниках — низ потолка; низ плиты перекрытия +2,700. Марка потолка — одна конструкция и отметка на весь альбом.
2. Потолки ГКЛ — каркасная система П113: подвесы через 1000, несущие профили через 500, основные через 1200 мм; листы — поперёк несущих профилей. В помещениях 2, 7 — ГКЛВ на оцинкованном каркасе.
3. Нижний уровень — пояс-короб по периметру шириной 300 мм (карниз подсветки + 150 мм полки), верхний — поле внутри пояса.
4. LED-лента в алюминиевом профиле посередине карниза короба шириной 300 мм (узел 1, лист 45); длина по плану: пом. 1 — 15,5 м (в плане освещения 15,5); пом. 4 — 12,3 м (в плане освещения 12,3); пом. 6 — 22,1 м (в плане освещения 22,1).
5. Ниши под шторы 150×120 мм — на всю длину стены с окном; карниз — на закладной до обшивки (узел 2, лист 45).
6. Примыкание к стенам: теневой шов 15 мм, техзазор 3 мм — пом. 1, 4, 6, по стенам, выровненным штукатуркой (узел 1); пом. 2, 5, 7, 8 разделительная лента.
7. Светильники и потолочные устройства — подложка с планов освещения, слаботочных систем и вентиляции (положение — по ним); вырезы и закладные — по ведомости на листе, до обшивки; отверстия не совмещать с профилями, глубина корпуса светильника до 70 мм.
8. Разрезы 1–1, 2–2 и узлы — на листе 45; высоты мебели и дверных блоков сверены с низом потолка в разрезах.
9. Шпаклевание ГКЛ и условия приёмки — Q3: рассеянный дневной свет, осмотр с 2 м; боковой свет не оценивается.
10. Люки ревизии 300×300 мм — по центру блоков питания LED (БП1, БП2, БП4; координаты — план освещения).
11. Пом. 3 — потолок по плите без подвесной системы; отделка — по ведомости отделки.

1000 мм · печать 1:1

| Изм. | Кол.уч | Лист | № док. | Подп. | Дата |
|---|---|---|---|---|---|
| Разраб. | | Кырпан А.С. | | | 05.10.26 |
| Пров. | | | | | |
| ГИП | | | | | |
| | | | | | |
| Н. контр. | | | | | |
| Утв. | | | | | |

**ГД-2026-003-АИ**

Трёхкомнатная квартира

Общая площадь 78,95* м² · * размеры со скана, не замерены (реестр — п. 6–11, К-13)

Дизайн-проект интерьера трёхкомнатной квартиры

| Стадия | Лист | Листов |
|---|---|---|
| РП | 44 | 94 |

**План потолков**

М 1:100

Кырпан Александр Сергеевич

выпуск 05.10.2026 № 6add39a08d · стр. 52 из 137

# Разрезы и узлы потолков

Разрезы по потолкам с отметками уровней · узлы коробов и ниш · размеры в мм

### Разрез 1–1 (М 1:40)

Пом. 6 Кухня-гостиная; линия разреза — план потолков, лист 44

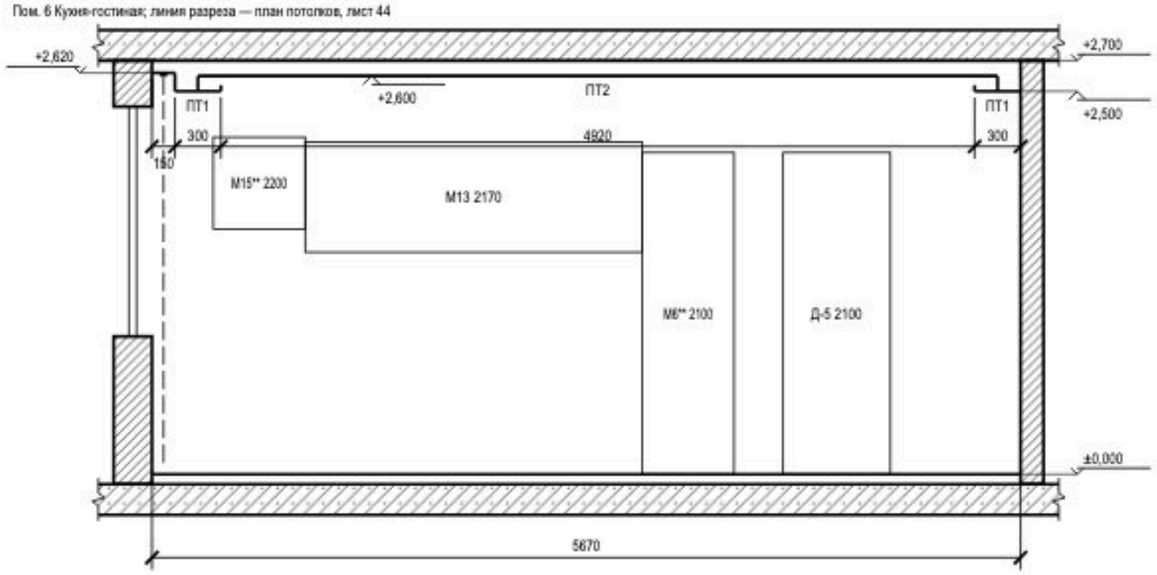


### Разрез 2–2 (М 1:40)

Пом. 1 Спальня 1; линия разреза — план потолков, лист 44

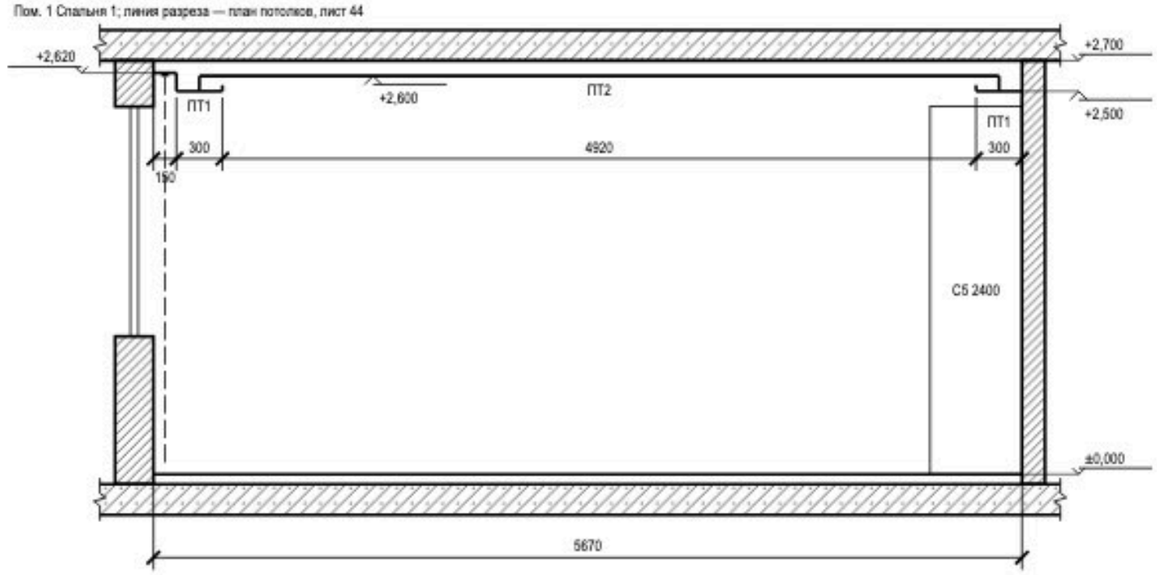


### 1 Короб с LED-подсветкой, теневой шов (М 1:10)

Пом. 1, 4, 6; карниз 150×100, щель под свет 60 мм

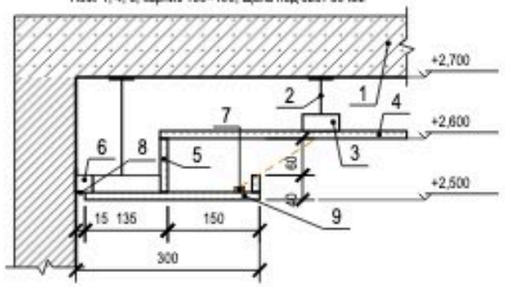


1 — плита перекрытия
2 — подвес прямой, шаг 1000 мм
3 — ПП 60×27: несущие через 500, основные через 1200 мм
4 — ГКЛ 12,5 по П113 — верхний уровень
5 — задняя стенка и бортик карниза — ГКЛ 12,5
6 — ПН 28×27 по периметру, к стене через 500 мм
7 — LED-лента в алюминиевом профиле
8 — теневой профиль: шов 15 мм, зазор 3 мм
9 — низ короба — ГКЛ 12,5 по ПП 60×27

### 2 Ниша под шторы (М 1:10)

Пом. 1, 4, 6; без подсветки; закладные под карниз — до обшивки

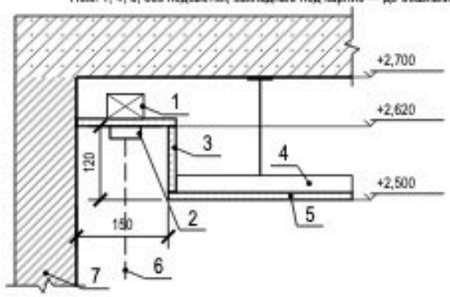


1 — закладная под карниз — брус 40×50
2 — карниз (шина), высота с верхом портьеры 100 мм
3 — стенка и потолок ниши — ГКЛ 12,5
4 — ПП 60×27 — каркас короба
5 — низ короба нижнего уровня — ГКЛ 12,5
6 — портьера
7 — стена с окном

## Условные обозначения

- плита перекрытия в сечении
- стена в сечении
- потолок ГКЛ в сечении; под линией — марка потолка (план потолков)
- мебель и дверные проёмы за секущей плоскостью; число — марка и верх от чистого пола, мм
- портьера в нише под шторы

**Допущения и предложения на листе**

Основа листа: размеры сняты со скана плана заказчика по размерным цепочкам, контрольный обмер на объекте не выполнялся (К-13); высота потолка 2700 мм принята: на плане заказчика не указана (К-11); толщины стен приняты: наружные 250 мм, перегородки 150 мм (на плане 85–190 мм) (К-13); разрешённая мощность 15 кВт принята по типовой квартире, технических условий нет (К-14); утолщение стены 190 × 1360 мм и элемент 1470 × 160 мм плана заказчика не определены (К-12); ниши санузла 2 закрыты перегородкой и фальш-стеной: проектное решение, на плане заказчика ниша у входа открыта (К-18); несущие стены не определены: до технического заключения все существующие стены считаются несущими (К-20); окна существующие и сохраняются; подоконная доска и глубина откосов не заданы — приняты, не замерены (К-27).

Знак «**» — предложение проектировщика, заказчиком не утверждено (согласовать с заказчиком): ИЗ-5, К-8: М6, М15.

См. лист открытых вопросов (лист 6, записи К-8, К-11; лист 7, записи К-12–К-14, К-18, К-20; лист 8, запись К-27; лист 9, запись ИЗ-5).

## Примечания

1. Разрезы — по линиям 1–1, 2–2 на плане потолков (лист 44). Отметки — от ±0,000 чистого пола, м; размеры — мм.
2. Высоты мебели и дверных блоков за секущей плоскостью сверены с низом потолка над ними: верх ниже низа короба и поля.
3. ГКЛ 12,5 мм по каркасу П113; перепад уровней и бортик карниза — ГКЛ по ПП 60×27 (узел 1). Ниша под шторы — на всю длину стены с окном, карниз на закладной до обшивки (узел 2).
4. Толщины плит перекрытия и пирога пола показаны условно.

1000 мм · печать 1:1

| Изм. | Кол.уч | Лист | № док. | Подп. | Дата |
|---|---|---|---|---|---|
| Разраб. | | Кырпан А.С. | | | 05.10.26 |
| Пров. | | | | | |
| ГИП | | | | | |
| Н. контр. | | | | | |
| Утв. | | | | | |

**ГД-2026-003-АИ**

Трёхкомнатная квартира

Общая площадь 78,95* м² · * размеры со скана, не замерены (реестр — л. 6–11, К-13)

Дизайн-проект интерьера трёхкомнатной квартиры

| Стадия | Лист | Листов |
|---|---|---|
| РП | 45 | 94 |

**Разрезы и узлы потолков**

М 1:40; 1:10

Кырпан Александр Сергеевич

выпуск 05.10.2026 · 6add39ab8d · стр. 53 из 137

# Раскладка плитки. Планы полов

Раскладка от чистовых размеров · размеры в мм · отметки от ±0,000

ПРЕДВАРИТЕЛЬНО · не для производства работ · открыто пунктов: 31 (реестр — л. 6–11)

**Фрагмент 1. Ванная (пом. 2). Пол 600×600, шов 2 мм, М 1:20**

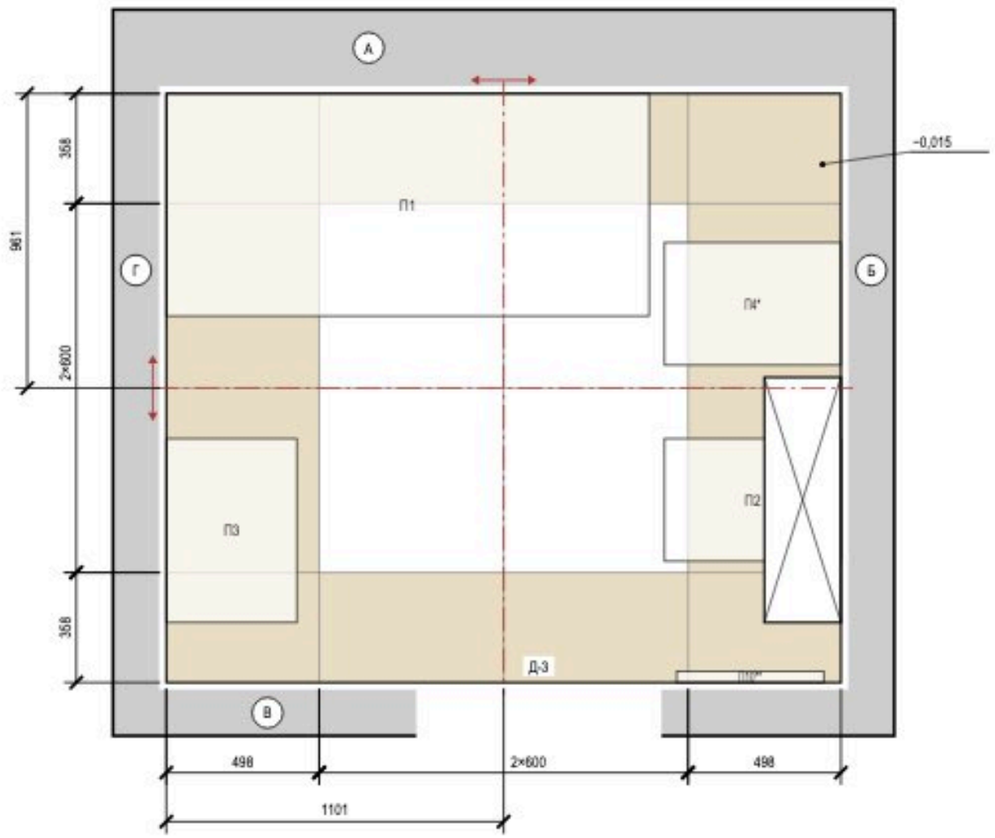


**Фрагмент 2. Санузел 2 (пом. 7). Пол 600×600, шов 2 мм, М 1:20**

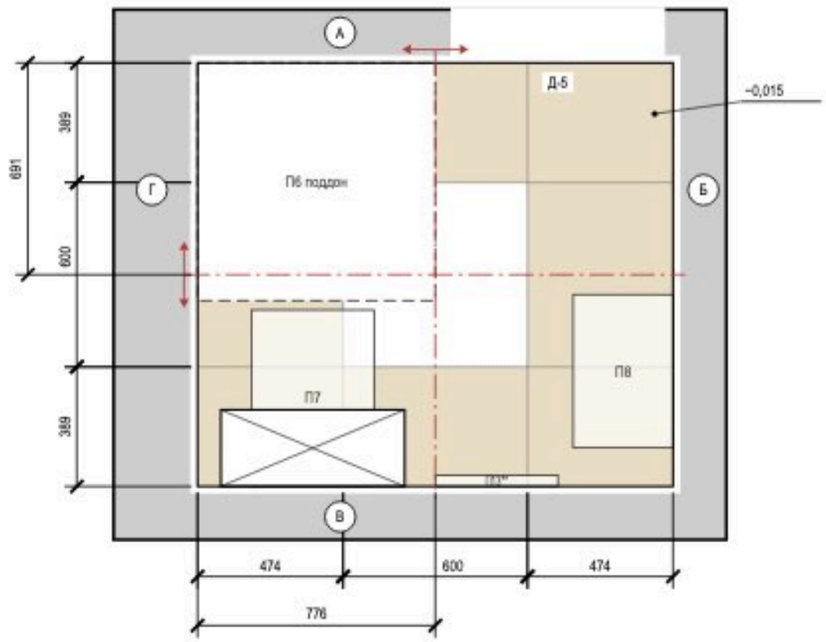


## Примечания

1. Раскладка от чистовых размеров: стены санузлов теряют 10 + 5 + 9 = 24 мм на сторону (штукатурка, клей, плитка); подрезки — чистые, без шва.
2. Старт — от центра помещения (штрихпунктир, стрелки направление укладки); размер старта — от чистовых стен Г и А.
3. Раскладка пола «Прихожая» и фартука «Кухня-гостиная» на листе «Раскладка плитки. Прихожая. Фартук кухни».
4. Калибр партии не задан — до укладки замерить (рабочий размер W, ГОСТ 13996-2019) и пересчитать подрезки.
5. Количество: целые по раскладке + по одной на подрезку, запас 10 %; один артикул — одна партия и тон. Исключены поддон, короб, проёмы и места за коробом; S — по чистым граням: стены нетто = зона облицовки по ведомости отделки − место за коробом инсталляции 1,68 м² (плитку за коробом не кладут), короб — отдельной строкой.
6. Клей C2 TE S1 Ceresit CM 17; C2 TE S1 (ГОСТ Р 56387-2018), затирка CG2WA Mapei Ultracolor Plus 132; CG2WA; расход — по ТУ выбранной марки.
7. Гидроизоляция: пол и стены 200 мм от ЧП; над ванной до 2000 и 300 мм за борт, у душа — до 2000 и 500 мм за поддон (см. развёртки); акт скрытых работ, пролив 24 ч.
8. Швы пола совмещены со швами стены А; по периметру демпферная лента.
9. Отметка чистого пола −0,015, порог 15 мм; стык с соседним покрытием — по оси полотна двери.

## Ведомость материалов

| Материал | Класс, код | Норма расхода | Кол-во |
|---|---|---|---|
| Затирка | CG2WA Mapei Ultracolor Plus 132 | (a+b)/ab·шов·t·1,6 | 3,1 кг |
| Затирка | CG2WA | (a+b)/ab·шов·t·1,6 | 0,7 кг |
| Клей | C2 TE S1 Ceresit CM 17 | 1,5 кг/м²·мм, слой 5 | 312 кг (13 меш.) |
| Клей | C2 TE S1 | 1,5 кг/м²·мм, слой 5 | 73 кг (3 меш.) |
| Гидроизоляция | обмазочная, 2 слоя: пол, стены по периметру и зоны замачивания | по ТУ | 20,0 м² |
| Демпф. лента | по периметру пола из плитки | | 22,4 м |

## Ведомость плитки

| Помещение, поверхность | Плитка, код | Формат | Шов | S, м² | Целых | Подр. | С запасом |
|---|---|---|---|---|---|---|---|
| Ванная, пол | аналог: керамогранит под травертин | 600×600 | 2 | 4,43 | 4 | 12 | 18 |
| Ванная, стены А–Г | аналог: керамогранит под травертин | 600×1200 | 2 | 17,65 | 10 | 21 | 35 |
| Ванная, короб инсталляции | аналог: керамогранит под травертин | 600×1200 | 2 | 1,76 | 0 | 6 | 7 |
| Санузел 2, пол | аналог: керамогранит под травертин | 600×600 | 2 | 2,29 | 0 | 8 | 9 |
| Санузел 2, стены А–Г | аналог: керамогранит под травертин | 600×1200 | 2 | 12,38 | 5 | 19 | 28 |
| Санузел 2, короб инсталляции | аналог: керамогранит под травертин | 600×1200 | 2 | 1,47 | 1 | 3 | 5 |
| Прихожая, пол | аналог: керамогранит ректифицированный под травертин, матовый | 600×1200 | 2 | 7,13 | 2 | 10 | 14 |
| Кухня-гостиная, фартук (ст. В) | аналог: керамогранит под травертин, матовый | 1200×600 | 2 | 1,87 | 0 | 4 | 5 |
| Итого 600×600 | | | | 6,72 | 4 | 20 | 27 |
| **Итого 600×1200** | | | | **42,26** | **18** | **63** | **94** |

## Условные обозначения

- плитка целая; тонкая линия — шов
- плитка с подрезкой (размер — на цепочке)
- ось старта; стрелки — направление укладки
- сантехприбор: габарит, высота по практике
- поддон душа — плитку пола под ним не кладут
- короб инсталляции: плитка пола — до короба
- отметка чистого пола на полке выноском, м
- (А) обозначение стены А–Г (как на развёртках)

Допущения и предложения на листе. Знак «*» принято (замерить). Знак «**» предложено (согласовать): пол пом. 2, 7, стены пом. 2, 7. См. лист открытых вопросов (листы 6–11).

1000 мм · печать 1:1

| Изм. | Кол.уч | Лист | № док. | Подп. | Дата |
|---|---|---|---|---|---|
| Разраб. | | Кырпан А.С. | | | 05.10.26 |
| Пров. | | | | | |
| ГИП | | | | | |
| | | | | | |
| Н. контр. | | | | | |
| Утв. | | | | | |

**ГД-2026-003-АИ**

Трёхкомнатная квартира

Общая площадь 78,95* м² · * размеры со скана, не замерены (реестр — п. 6–11, К-13)

Дизайн-проект интерьера трёхкомнатной квартиры

| Стадия | Лист | Листов |
|---|---|---|
| РП | 46 | 94 |

**Раскладка плитки. Планы полов**

М 1:20

**Кырпан Александр Сергеевич**

выпуск 05.10.2026 · 6add39ab8d · стр. 54 из 137

# Раскладка плитки. Прихожая. Фартук кухни

ПРЕДВАРИТЕЛЬНО · не для производства работ · открыто пунктов: 31 (реестр — л. 6–11)

Раскладка от чистовых размеров · размеры в мм · высоты фартука от чистого пола

**Фрагмент 1. Прихожая (пом. 5). Пол 600×1200, шов 2 мм, М 1:20**

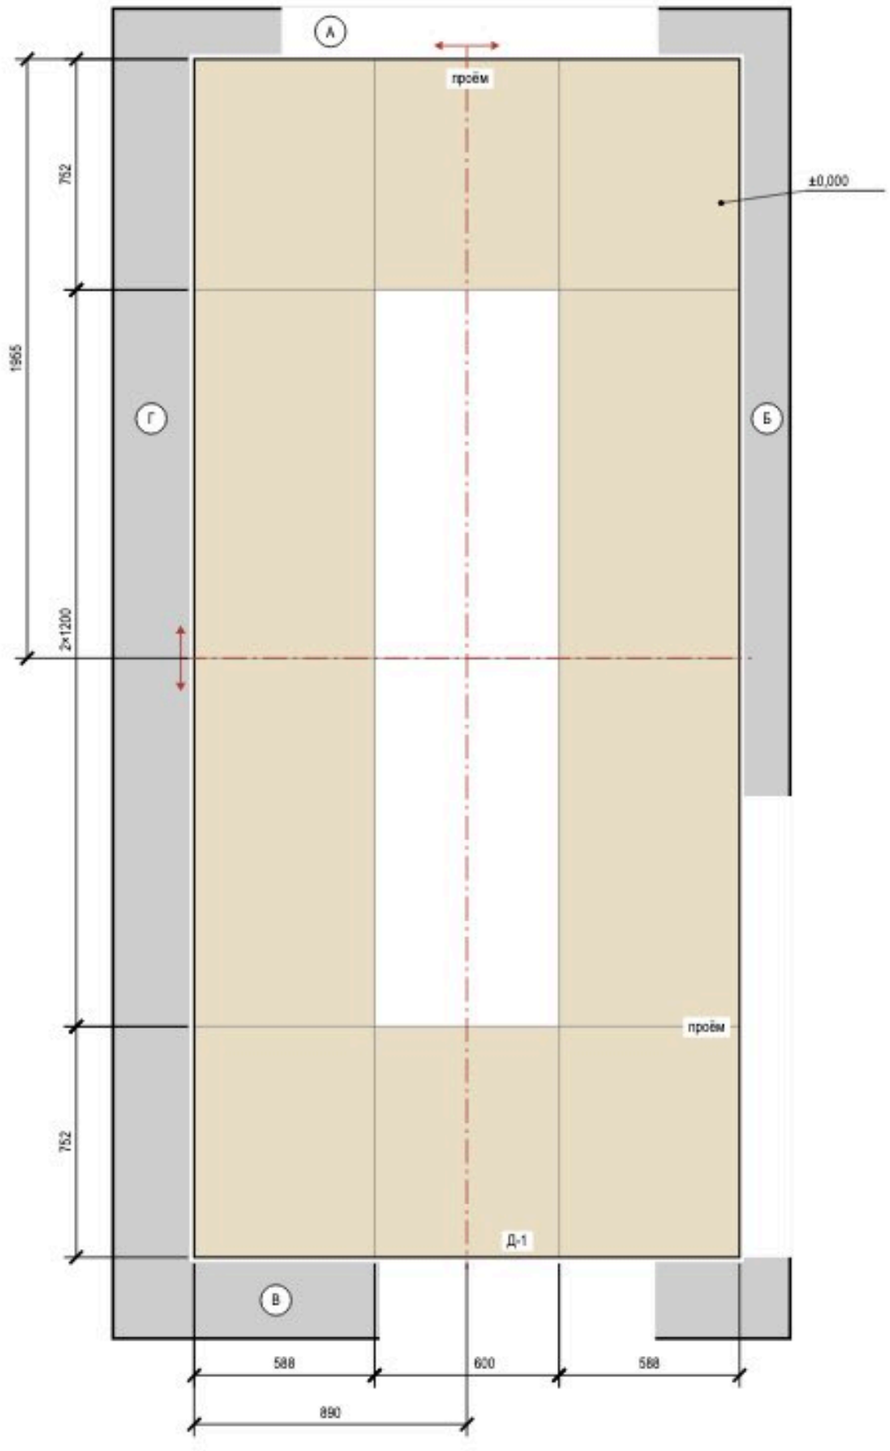


**Фрагмент 2. Кухня-гостиная (пом. 6), фартук, стена В. 1200×600, шов 2 мм, М 1:20**

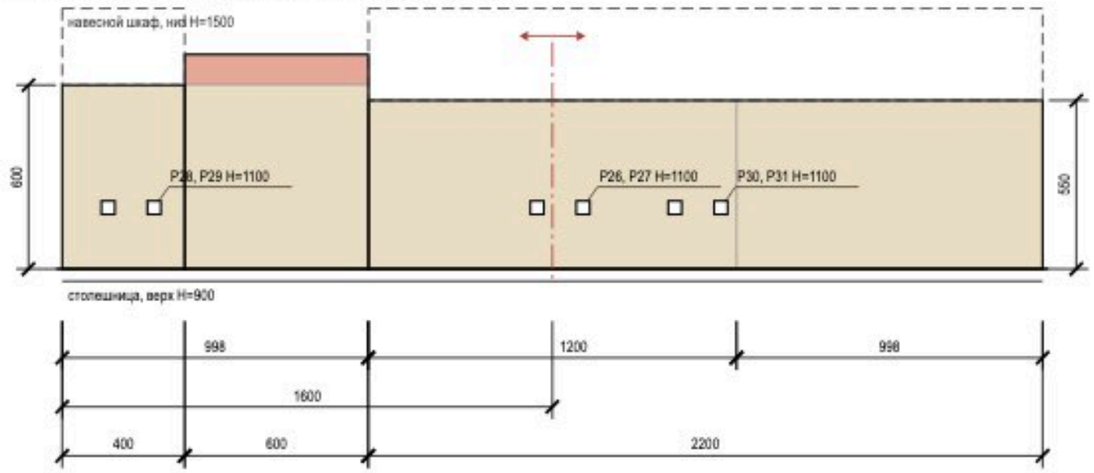


## Условные обозначения

- плитка целая; тонкая линия — шов
- плитка с подрезкой (размер — на цепочке)
- ось старта; стрелки — направление укладки
- электроточка: марка и H — по листам ЭОМ
- столешница (верх)
- навесной шкаф над фартуком
- отметка чистого пола на полке выноски, м
- (А) обозначение стены А–Г (как на развёртках)

## Подсчёт плитки

| Поверхность | Формат | S, м² | Целых | Подр. | С запасом |
|---|---|---|---|---|---|
| Прихожая, пол | 600×1200 | 7,13 | 2 | 10 | 14 |
| Кухня-гостиная, фартук (ст. В) | 1200×600 | 1,87 | 0 | 4 | 5 |

## Сдвиг розеток фартука под раскладку

| Точка (ЭОМ) | Проект: от угла / H | Под раскладку: от угла / H | Сдвиг, мм |
|---|---|---|---|
| P26, P27, P30, P31 | 1700, 1550, 2150, 2000 / 1100 | 1700, 1550, 2150, 2000 / 1175 | H +75 — ось ряда |
| P28, P29 | 300, 150 / 1100 | 300, 150 / 1200 | H +100 — ось ряда |

## Примечания

1. Прихожая: керамогранит 600×1200, длинная сторона — вдоль стен Б и Г, шов 2 мм, прямая раскладка от центра. Стены окрашены: раскладка от чистового контура минус штукатурка и шпаклёвка 15 мм на сторону (принято); подрезки 588 / 752 мм, срез — под плинтус.
2. Прихожая: деформационный зазор по периметру 8–10 мм под плинтусом; в проёмах — стык с соседним покрытием по оси полотна двери. Клей C2 TE S1, затирка CG2WA.
3. Фартук, Кухня-гостиная: 1200×600 горизонтально, шов 2 мм; зоны 2200 мм — 900…1450, 600 мм — 900…1600, 400 мм — 900…1500 (от столешницы до низа навесного шкафа, без шкафа — 700 мм). Старт от центра участка, подрезки 998 мм. Площадь 1,87 м² — как в ведомости отделки.
4. Фартук — после монтажа столешницы, низ на 2–3 мм выше неё, шов со столешницей — санитарный герметик; навесные шкафы — после фартука. Торцы у пенала и стены — профиль или запил 45°.
5. Фартук, Кухня-гостиная: в зоне до отм. 1600 верхний ряд подрезан 98 мм — меньше 1/3 плитки; полоса прикрыта корпусом навесного модуля и на виду не остаётся. Раскладкой не снимается: убрать подрезку можно, только выровняв низ этого модуля с соседними (1450 мм) — решение мебельщика.
6. Розетки из таблицы переносятся до черновой электрики: по высоте — на ось ряда плитки, от вертикального шва крупной плитки — не ближе 60 мм. Привязка — от левого края фартука на развёртке.
7. Клей, затирка и итог по форматам — в ведомостях листа «Раскладка плитки. Планы полов».

Допущения и предложения на листе. Знак «*» предложено (согласовать): пол пом. 5, 6, плинтус пом. 5, 6, фартук пом. 6. См. лист открытых вопросов (листы 6–11).

1000 мм · печать 1:1

| Изм. | Кол.уч | Лист | № док. | Подп. | Дата |
|---|---|---|---|---|---|
| Разраб. | | Кырлан А.С. | | | 05.10.26 |
| Пров. | | | | | |
| ГИП | | | | | |
| | | | | | |
| Н. контр. | | | | | |
| Утв. | | | | | |

**ГД-2026-003-АИ**

Трёхкомнатная квартира

Общая площадь 78,95* м² · * размеры со скана, не замерены (реестр — л. 6–11, К-13)

Дизайн-проект интерьера трёхкомнатной квартиры

| Стадия | Лист | Листов |
|---|---|---|
| РП | 47 | 94 |

**Раскладка плитки. Прихожая. Фартук кухни**

М 1:20

Кырлан Александр Сергеевич

выпуск 05.10.2026 № 6add3ab8d · стр. 55 из 137

# Раскладка плитки. Ванная. Развёртки стен

ПРЕДВАРИТЕЛЬНО · не для производства работ · открыто пунктов: 31 (реестр — л. 6–11)

Пом. 2 · вид изнутри помещения · размеры в мм · высоты от чистого пола, отметки от ±0,000

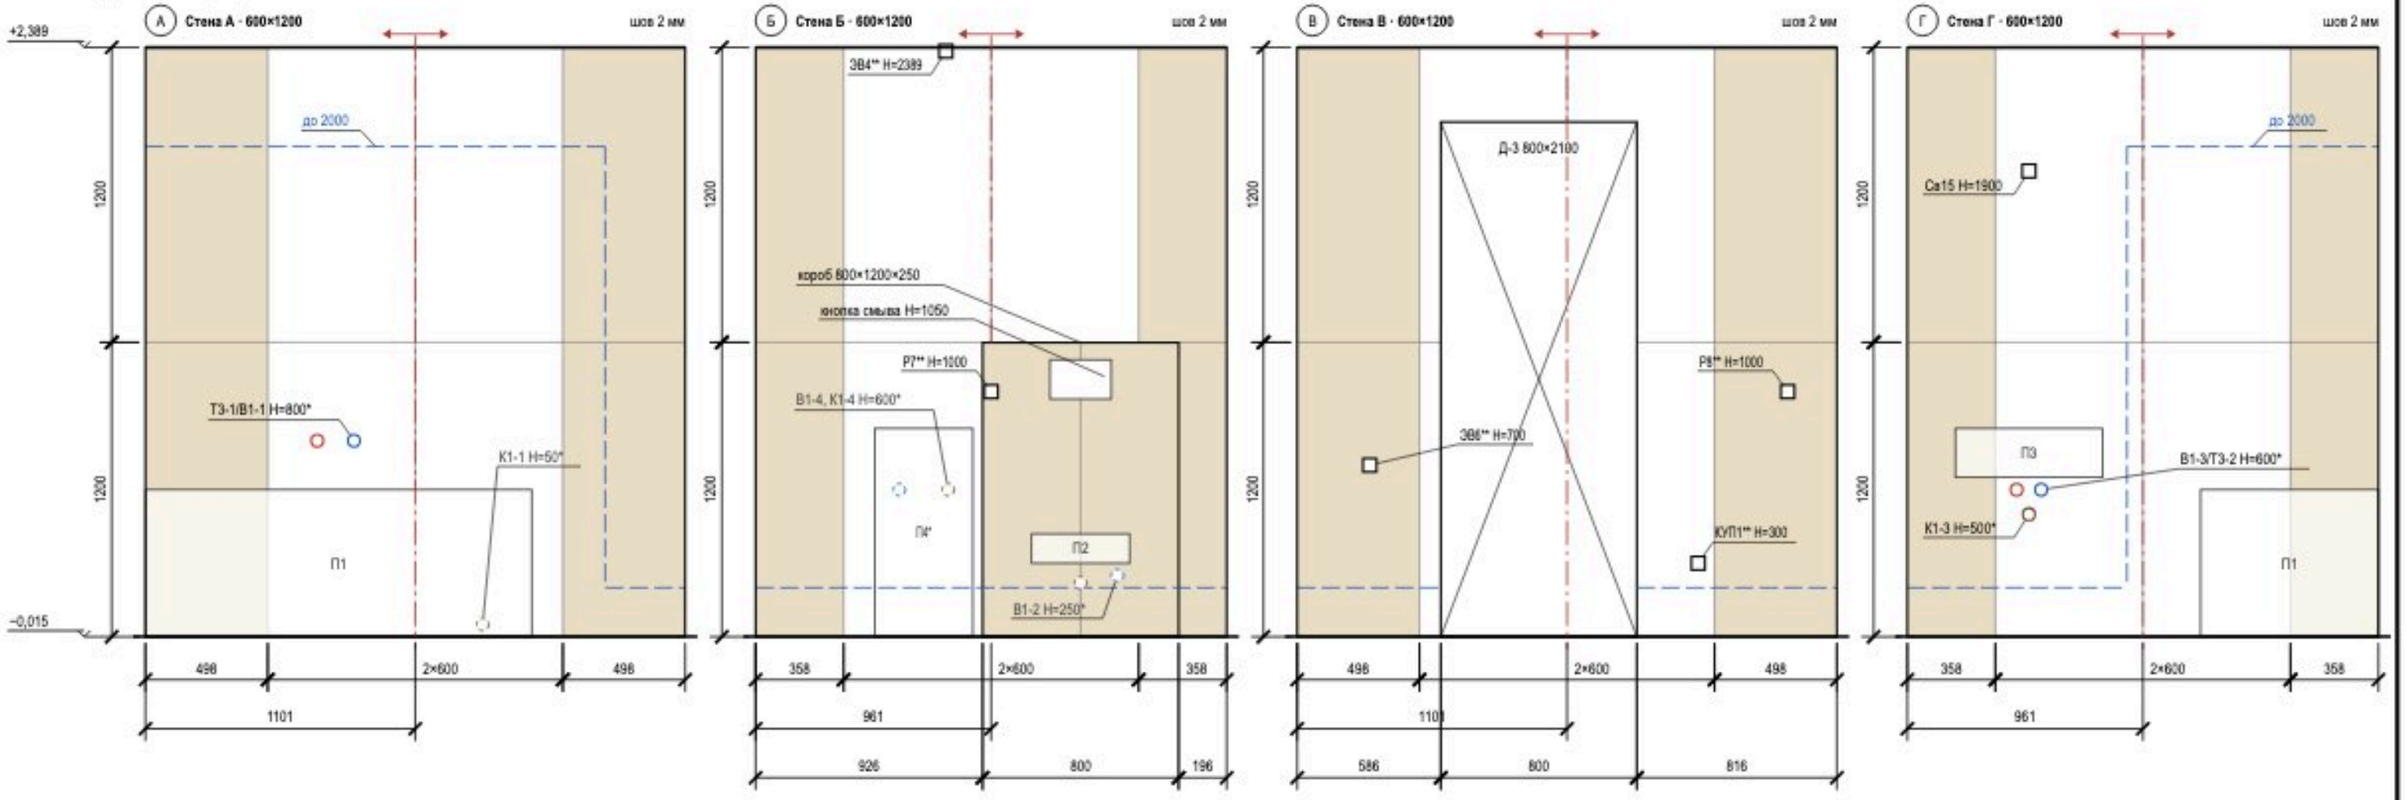


## Подсчёт плитки по стенам и коробу

| Поверхность | L × H, мм | S, м² | Целых | Подр. | С запасом | Подрезки: край / верх, мм |
|---|---|---|---|---|---|---|
| стена А | 2202 × 2404 | 5,41 | 4 | 4 | 9 | 498 / 498; целый ряд |
| стена Б | 1922 × 2404 | 3,78 | 2 | 5 | 8 | 358 / 358; целый ряд |
| короб (ст. Б) | 800×1200×250 | 1,76 | 0 | 6 | 7 | лицо 399 / 399; бок. 250 |
| стена В | 2202 × 2404 | 3,73 | 0 | 8 | 9 | 498 / 498; целый ряд |
| стена Г | 1922 × 2404 | 4,74 | 4 | 4 | 9 | 358 / 358; целый ряд |
| **Итого** | | **19,41** | **10** | **27** | **42** | |

## Сдвиг точек под раскладку

| Точка (ВК, ЭОМ) | Стена | Проект: от угла / Н | Под раскладку: от угла / Н | Сдвиг, мм |
|---|---|---|---|---|
| Т3-1/В1-1 | А | 776 / 800 | 800 / 800 | +24 в центр плитки |
| ЭВ4** | Б | 776 / 2389 | 660 / 2403 | −116 в центр плитки; Н +14 |
| КУП1** | В | 1636 / 300 | 1703 / 300 | +67 на шов |
| ЭВ6** | В | 296 / 700 | 198 / 700 | −98 в центр плитки |
| В1-3/Т3-2, К1-3, Са15 | Г | 496 / 600, 500, 1900 | 359 / 600, 500, 1900 | −137 на шов |

## Примечания

1. Вид изнутри, стены по часовой стрелке А → Г. Высоты — от чистого пола (−0,015), отметки — от ±0,000. Раскладка от чистовых размеров (штукатурка 10 + клей 5 + плитка 9 мм), подрезки чистые; старт — от оси стены, ряды от пола целыми.
2. Облицовка до потолка (+2,389).
3. Точки из таблицы сдвигов переносятся до черновой разводки: смеситель — по оси пары В1 + Т3; вывод на ось прибора — вместе с прибором, иначе старт раскладки на ось прибора.
4. Выводы — по «Плану выводов сантехники», электроточки — по ЭОМ. «*» — высота по практике; за приборами и в коробе (К1-1, В1-2, К1-2, В1-4, К1-4) — штриховым кольцом.
5. Гидроизоляция: 200 мм от ЧП по периметру; над ванной — до 2000 и 300 мм за борт (СП 29.13330.2011, п. 7.2 — на высоту замачивания); углы — лентой; акт скрытых работ, пролив.
6. Короб 800×1200×250: лицо 399 / 399 мм от оси кнопки смыва, боковины, полка; углы — запил 45° или профиль; за коробом плитку не кладут.
7. Между коробом и углом полоса 196 мм — довести короб до угла.

## Условные обозначения

- плитка целая; тонкая линия — шов
- плитка с подрезкой (размер — на цепочке)
- ось старта; стрелки — направление укладки
- верх гидроизоляции: 200 от ЧП, в мокрой зоне — «до …»
- проём — не облицовывается
- сантехприбор: габарит, высота по практике
- короб инсталляции, в нём кнопка смыва 250×160
- вывод В1 (код — в ведомости привязок)
- вывод Т3 (код — в ведомости привязок)
- вывод К1 (код — в ведомости привязок)
- вывод за прибором / в коробе (не на сетке)
- электроточка: марка и Н — по листам ЭОМ
- отметка уровня, м: ±0,000 — чистый пол жилых помещений
- низ потолка; серая полоса — стена без плитки
- обозначение стены А–Г (как на развёртках)

Допущения и предложения на листе. Знак «*» принято (замерить): отметка существующего пола. Знак «**» предложено (согласовать): пол пом. 2, стены пом. 2. См. лист открытых вопросов (листы 6–11).

1000 мм · печать 1:1

| Изм. | Кол.уч | Лист | № док. | Подп. | Дата |
|---|---|---|---|---|---|
| Разраб. | | Кырпан А.С. | | | 05.10.26 |
| Пров. | | | | | |
| ГИП | | | | | |
| | | | | | |
| Н. контр. | | | | | |
| Утв. | | | | | |

**ГД-2026-003-АИ**

Трёхкомнатная квартира

Общая площадь 78,95* м² · * размеры со скана, не замерены (реестр — п. 6–11, К-13)

Дизайн-проект интерьера трёхкомнатной квартиры

| Стадия | Лист | Листов |
|---|---|---|
| РП | 48 | 94 |

Раскладка плитки. Ванная. Развёртки стен

М 1:25

Кырпан Александр Сергеевич

выпуск 05.10.2026 · 6add39ab8d · стр. 56 из 137

# Раскладка плитки. Санузел 2. Развёртки стен

ПРЕДВАРИТЕЛЬНО · не для производства работ · открыто пунктов: 31 (реестр — л. 6–11)

Пом. 7 · вид изнутри помещения · размеры в мм · высоты от чистого пола, отметки от ±0,000

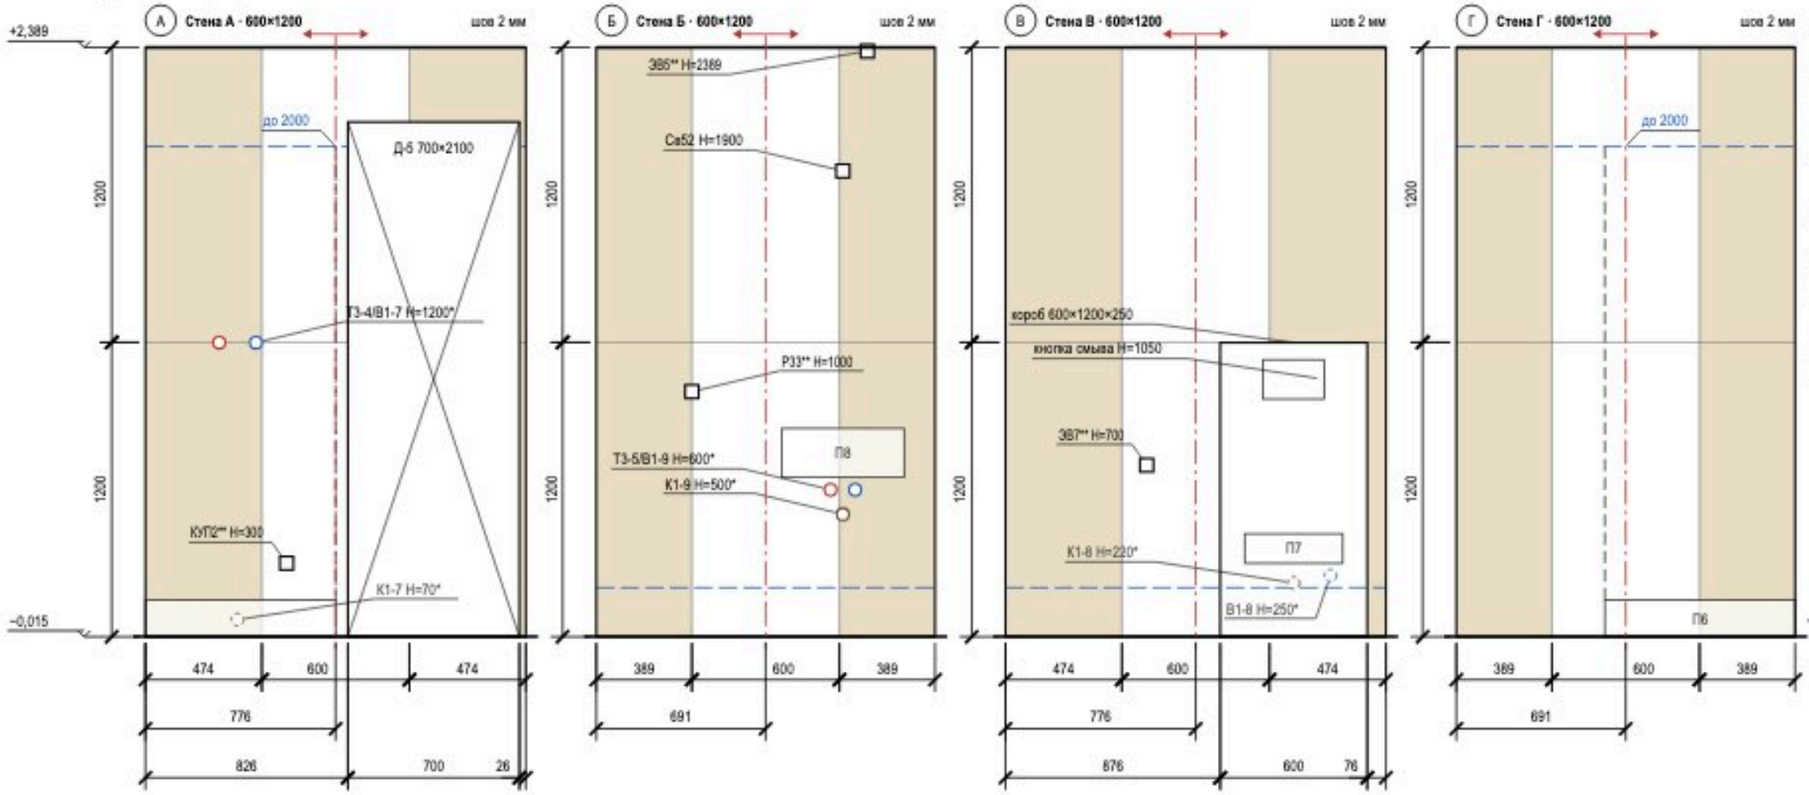


## Условные обозначения

- плитка целая; тонкая линия — шов
- плитка с подрезкой (размер — на цепочке)
- ось старта; стрелки — направление укладки
- верх гидроизоляции: 200 от ЧП, в мокрой зоне — «до …»
- проём — не облицовывается
- сантехприбор: габарит, высота по практике
- граница душевой зоны (ограждение)
- короб инсталляции, в нём кнопка смыва 250×160
- вывод В1 (код — в ведомости привязок)
- вывод Т3 (код — в ведомости привязок)
- вывод К1 (код — в ведомости привязок)
- вывод за прибором / в коробе (не на сетке)
- электроточка: марка и Н — по листам ЭОМ
- отметка уровня, м: ±0,000 — чистый пол жилых помещений
- низ потолка; серая полоса — стена без плитки
- (А) обозначение стены А–Г (как на развёртках)

## Подсчёт плитки по стенам и коробу

| Поверхность | L × H, мм | S, м² | Целых | Подр. | С запасом | Подрезки: край / верх, мм |
|---|---|---|---|---|---|---|
| стена А | 1552 × 2404 | 2,38 | 0 | 6 | 7 | 474 / 474; целый ряд |
| стена Б | 1382 × 2404 | 3,44 | 2 | 4 | 7 | 389 / 389; целый ряд |
| стена В | 1552 × 2404 | 3,13 | 1 | 5 | 7 | 474 / 474; целый ряд |
| короб (ст. В) | 600×1200×250 | 1,47 | 1 | 3 | 5 | лицо 600; бок. 250 |
| стена Г | 1382 × 2404 | 3,44 | 2 | 4 | 7 | 389 / 389; целый ряд |
| **Итого** | | **13,85** | **6** | **22** | **33** | |

## Сдвиг точек под раскладку

| Точка (ВК, ЭОМ) | Стена | Проект: от угла / Н | Под раскладку: от угла / Н | Сдвиг, мм |
|---|---|---|---|---|
| Т3-4/В1-7 | А | 376 / 1200 | 475 / 1141 | +99 на шов; Н −59 |
| КУП2** | А | 576 / 300 | 475 / 300 | −101 на шов |
| Т3-5/В1-9, К1-9, Са52 | Б | 1006 / 600, 500, 1900 | 992 / 600, 500, 1900 | −14 на шов |
| 389** | Б | 1106 / 2389 | 992 / 2343 | −114 на шов; Н −46 |
| 387** | В | 576 / 700 | 475 / 700 | −101 на шов |

## Примечания

1. Вид изнутри, стены по часовой стрелке А → Г. Высоты — от чистого пола (−0,015), отметки — от ±0,000. Раскладка от чистовых размеров (штукатурка 10 + клей 5 + плитка 9 мм), подрезки чистые; старт — от оси стены, ряды от пола целыми.
2. Облицовка до потолка (+2,389).
3. Точки из таблицы сдвигов переносятся до черновой разводки: смеситель — по оси пары В1 + Т3; вывод на оси прибора — вместе с прибором, иначе старт раскладки — на ось прибора.
4. Выводы — по «Плану выводов сантехники», электроточки — по ЭОМ, «*» — высота по практике; за приборами и в коробе (К1-7, В1-8, К1-8) — штриховым кольцом.
5. Гидроизоляция: 200 мм от ЧП по периметру; у душа — до 2000 и 500 мм за поддон (СП 29.13330.2011, п. 7.2 — на высоту замачивания); углы — лентой; акт скрытых работ, пролив.
6. Короб 600×1200×250: лицо 600 мм от оси кнопки смыва, боковины, полка; углы — запил 45° или профиль; за коробом плитку не кладут.
7. Между коробом и углом полоса 76 мм — довести короб до угла.

Допущения и предложения на листе. Основа листа: размеры сняты со скана плана заказчика по размерным цепочкам, контрольный обмер на объекте не выполнялся (К-13); высота потолка 2700 мм принята: на плане заказчика не указана (К-11); толщины стен приняты: наружные 250 мм, перегородки 150 мм (на плане 85–190 мм) (К-13); разрешённая мощность 15 кВт принята по типовой квартире, технических условий нет (К-14); утолщение стены 190 × 1360 мм и элемент 1470 × 160 мм плана заказчика не определены (К-12); ниши санузла 2 закрыты перегородкой и фальш-стеной: проектное решение, на плане заказчика ниша у входа открыта (К-18); несущие стены не определены: до технического заключения все существующие стены считаются несущими (К-20); окна существующие и сохраняются; подоконная доска и глубина откосов не заданы — приняты, не замерены (К-27). Знак «*» — принято, не замерено и не подтверждено (замерить на объекте); К-13: отметка существующего пола — отметка существующего пола и верха плиты не замерена: на плане заказчика отметок нет; нивелировка — в задании на обмер (К-13). Знак «**» — предложение проектировщика, заказчиком не утверждено (согласовать с заказчиком); ИЗ-2, К-2, К-23: пол пом. 7 — пирог пола: стяжка 33 мм и обмазочная гидроизоляция добавлены разработчиком проекта; артикул изделия не выбран: позиция описана характеристиками («каналог по характеристикам»), артикул выбирается при закупке; ИЗ-8: ЭВ5 — вывод к бытовому вентилятору, таймер выбега; КУП2 — коробка уравнивания потенциалов, проводник от шины РЕ; К-2, К-23: стены пом. 7 — артикул изделия не выбран: позиция описана характеристиками («каналог по характеристикам»), артикул выбирается при закупке. См. лист открытых вопросов (лист 6, записи К-2, К-7, К-11; лист 7, записи К-12–К-14, К-18, К-20; лист 8, записи К-23, К-27; лист 9, записи ИЗ-1, ИЗ-2, ИЗ-4, ИЗ-8, ИЗ-9); по листу — К-2, К-23.

1000 мм · печать 1:1

| Изм. | Кол.уч | Лист | № док. | Подп. | Дата |
|---|---|---|---|---|---|
| Разраб. | | Кырлан А.С. | | | 05.10.26 |
| Пров. | | | | | |
| ГИП | | | | | |
| | | | | | |
| Н. контр. | | | | | |
| Утв. | | | | | |

**ГД-2026-003-АИ**

Трёхкомнатная квартира

Общая площадь 78,95* м² · * размеры со скана, не замерены (реестр — п. 6–11, К-13)

| Дизайн-проект интерьера трёхкомнатной квартиры | Стадия | Лист | Листов |
|---|---|---|---|
| | РП | 49 | 94 |
| **Раскладка плитки. Санузел 2. Развёртки стен** М 1:25 | **Кырлан Александр Сергеевич** | | |

выпуск 05.10.2026 · 6add39ab8d · стр. 57 из 137

07

# Полы и отделка

Кырлан Александр Сергеевич

выпуск 05.10.2026 № 6add39ab8d · стр. 58 из 137

# План полов

Покрытия, направление укладки, отметки чистого пола, стыки · размеры в мм · отметки в м

ПРЕДВАРИТЕЛЬНО · не для производства работ · открыто пунктов: 31 (реестр — л. 6–11)

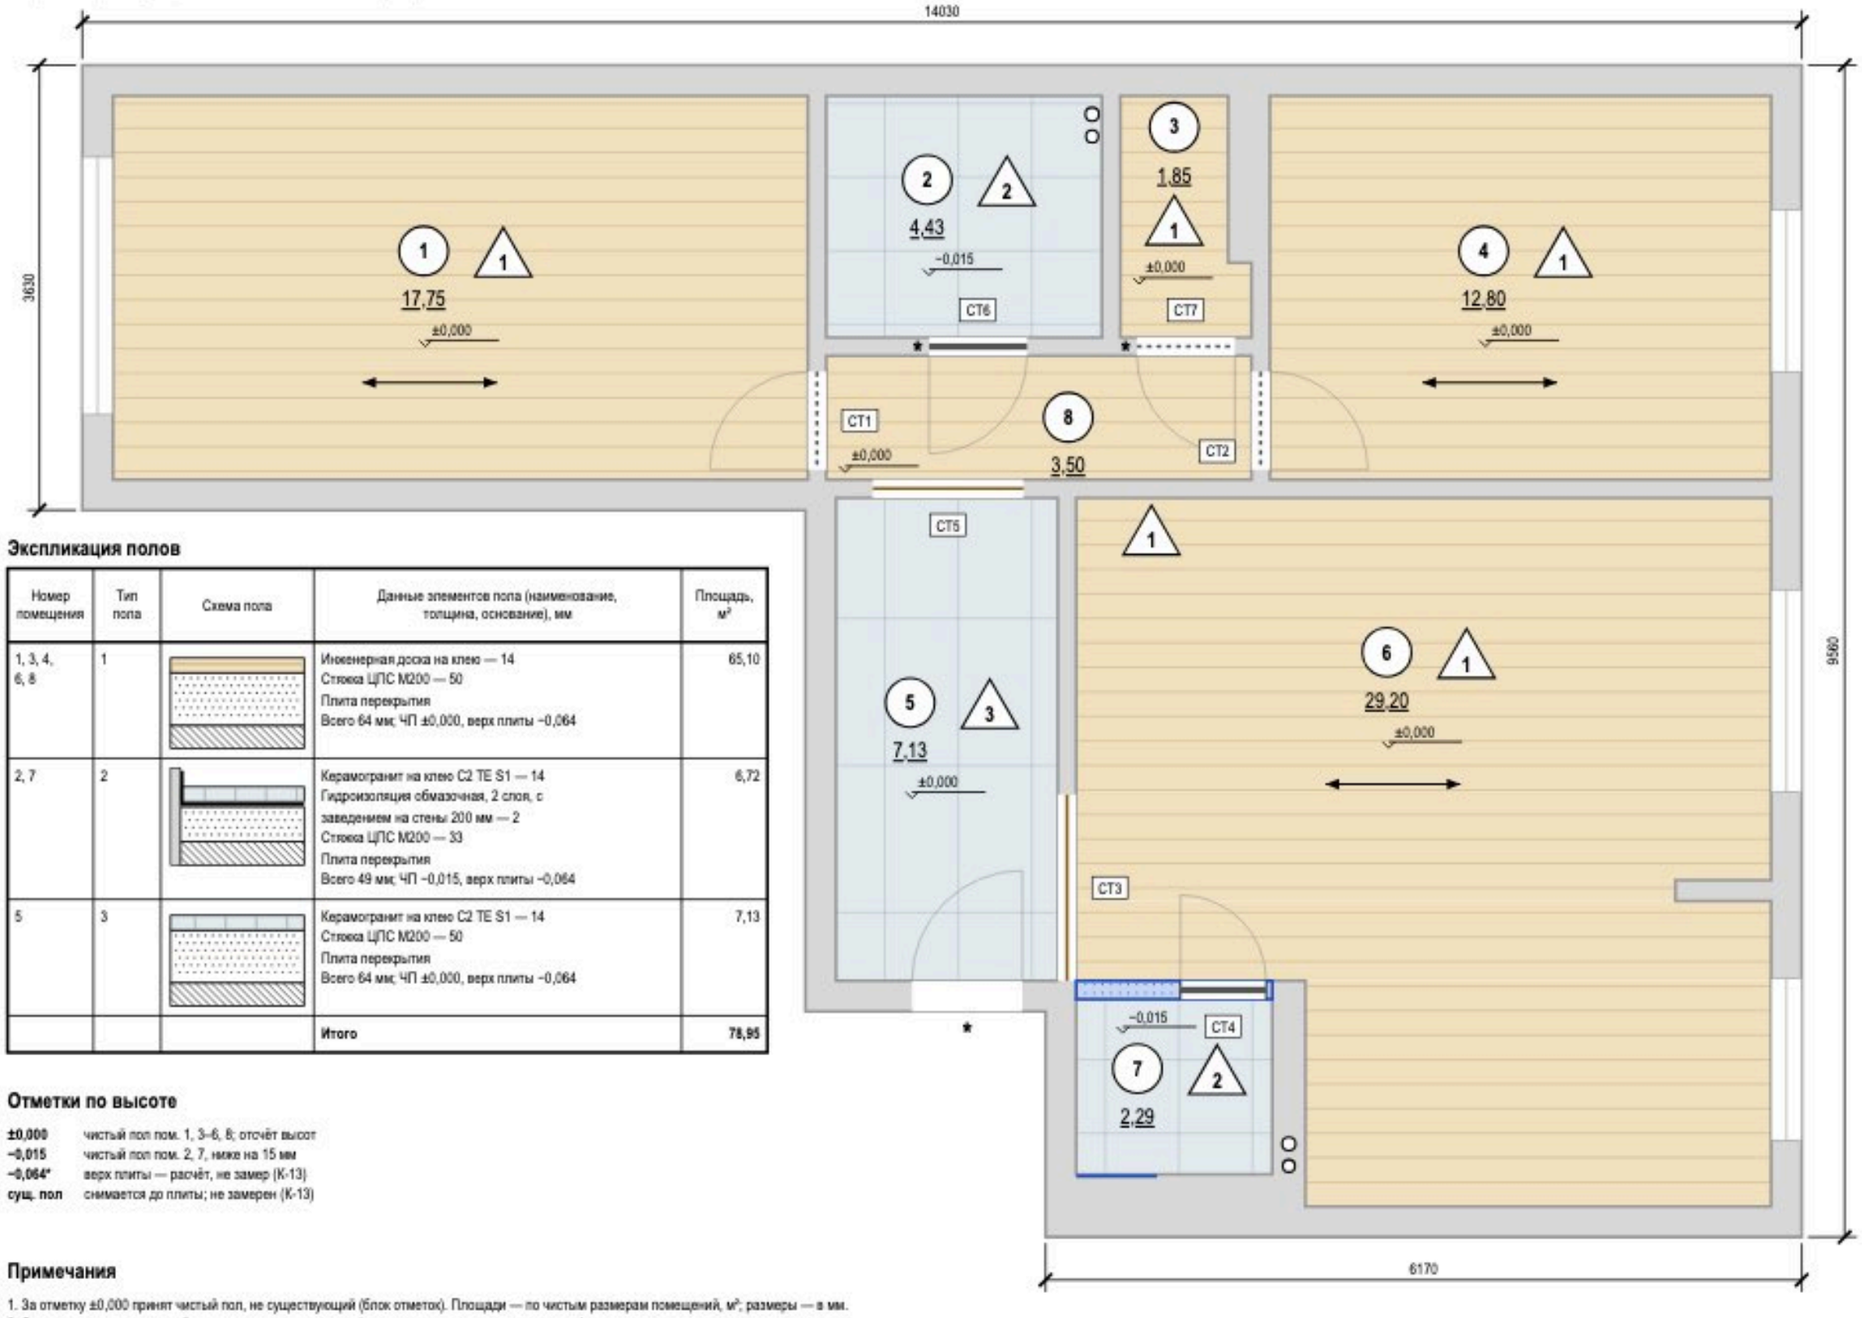


## Экспликация полов

| Номер помещения | Тип пола | Схема пола | Данные элементов пола (наименование, толщина, основание), мм | Площадь, м² |
|---|---|---|---|---|
| 1, 3, 4, 6, 8 | 1 | | Инженерная доска на клею — 14<br>Стяжка ЦПС М200 — 50<br>Плита перекрытия<br>Всего 64 мм; ЧП ±0,000, верх плиты −0,064 | 65,10 |
| 2, 7 | 2 | | Керамогранит на клею С2 TE S1 — 14<br>Гидроизоляция обмазочная, 2 слоя, с заведением на стены 200 мм — 2<br>Стяжка ЦПС М200 — 33<br>Плита перекрытия<br>Всего 49 мм; ЧП −0,015, верх плиты −0,064 | 6,72 |
| 5 | 3 | | Керамогранит на клею С2 TE S1 — 14<br>Стяжка ЦПС М200 — 50<br>Плита перекрытия<br>Всего 64 мм; ЧП ±0,000, верх плиты −0,064 | 7,13 |
| | | | **Итого** | **78,95** |

## Отметки по высоте

**±0,000** чистый пол пом. 1, 3–6, 8; отсчёт высот
**−0,015** чистый пол пом. 2, 7, ниже на 15 мм
**−0,064*** верх плиты — расчёт, не замер (К-13)
**сущ. пол** снимается до плиты; не замерен (К-13)

## Примечания

1. За отметку ±0,000 принят чистый пол, не существующий (блок отметок). Площади — по чистым размерам помещений, м²; размеры — в мм.
2. Стык разнотипных покрытий — по оси дверного полотна (под полотном в закрытом положении); решение стыка — по ведомости стыков.
3. Пол санузлов ниже смежных помещений на 15 мм за счёт меньшей толщины стяжки (верх плиты общий — по экспликации полов); гидроизоляция по стяжке с заведением на стены не менее 200 мм (СП 29.13330.2011, п. 7.2), до облицовки — тест проливом и акт скрытых работ.
4. Трубопроводы в конструкции пола не прокладываются: пирог пола 49–64 мм не вмещает выпуски канализации с уклоном — выпуски К1 ведутся по стенам над чистым полом в коробах (лист 40).
5. Звукоизоляционный слой под стяжкой проектом не предусмотрен (стяжка по плите): приведённый уровень ударного шума перекрытия с полом $L_{nw}$ не более 60 дБ (СП 51.13330.2011, табл. 2) подтвердить по данным дома; при превышении — плавающая стяжка по звукоизоляции с демпферной лентой по контуру и у стояков, пирог пересчитать.
6. Штучные покрытия (инженерная доска): направление — по стрелке; влажность основания по СМ не более 2,0 % (по ТУ изготовителя).
7. Ровность основания — просвет под 2-метровой рейкой не более 2 мм: пом. 1, 3, 4, 6, 8 (инженерная доска), пом. 2, 5, 7 (керамогранит); проверить до укладки покрытия (СП 71.13330.2017, табл. 8.5).
8. Сетка на плитке — условная, в размер формата; точка старта и раскладка — по листу раскладки плитки.
9. Пироги полов — по экспликации полов: слои сверху вниз, толщины в мм; гидроизоляция мокрых зон — в пироге и в ведомости отделки; схема пола — без масштаба.

1000 мм · печать 1:1

Допущения и предложения на листе. Знак «*» принято (замерить): Ст К1-1, Ст В1-1, Ст К1-2, Ст В1-2, отметка существующего пола. Знак «**» предложено (согласовать): пол пом. 1–8, плинтус пом. 1, 3–6, 8, стены пом. 2, 7, фартук пом. 6, П-1, П-2. См. лист открытых вопросов (листы 6–11).

## Стыки покрытий в проёмах

| Марка | Проём | Типы пола | Отметки ЧП | Решение |
|---|---|---|---|---|
| СТ1 | 1–8 (Д-2) | 1 / 1 | ±0,000 / ±0,000 | б/п |
| СТ2 | 4–8 (Д-2) | 1 / 1 | ±0,000 / ±0,000 | б/п |
| СТ3 | 5–6 | 3 / 1 | ±0,000 / ±0,000 | Т-профиль |
| СТ4 | 6–7 (Д-5) | 1 / 2 | ±0,000 / −0,015 | порог h=15 мм |
| СТ5 | 8–5 | 1 / 3 | ±0,000 / ±0,000 | Т-профиль |
| СТ6 | 8–2 (Д-3) | 1 / 2 | ±0,000 / −0,015 | порог h=15 мм |
| СТ7 | 8–3 (Д-4) | 1 / 1 | ±0,000 / ±0,000 | б/п |

## Условные обозначения

- тип 1 — инженерная доска, линии — вдоль доски
- тип 2 — керамогранит 600×600, сетка — формат плитки
- тип 3 — керамогранит 600×1200, сетка — формат плитки
- 1 — номер типа пола (экспликация полов)
- схема пола, без масштаба: плита — штриховка, стяжка — точки, звукоизоляция — зигзаг, гидроизоляция — утолщённая линия с заведением на стену
- направление укладки (длинная сторона доски)
- отметка чистого пола, м
- стык в проёме: без порога (б/п)
- стык в проёме: Т-профиль по оси полотна
- стык в проёме: порог
- СТ1 — марка стыка (ведомость стыков)
- стояк: К1 — канализация, В1 — ХВС, Т3 — ГВС
- новое — возводится по проекту (синим)
- 1 — номер помещения, площадь м²

| Изм. | Кол.уч | Лист | № док. | Подп. | Дата |
|---|---|---|---|---|---|
| Разраб. | | Кырпан А.С. | | | 05.10.26 |
| Пров. | | | | | |
| ГИП | | | | | |
| | | | | | |
| Н. контр. | | | | | |
| Утв. | | | | | |

**ГД-2026-003-АИ**

Трёхкомнатная квартира

Общая площадь 78,95* м² · * размеры со скана, не замерены (реестр — л. 6–11, К-13)

Дизайн-проект интерьера трёхкомнатной квартиры

| Стадия | Лист | Листов |
|---|---|---|
| РП | 50 | 94 |

**План полов**

М 1:50

Кырпан Александр Сергеевич

выпуск 05.10.2026 · 6add39ab8d · стр. 59 из 137

# Ведомость отделки помещений

Потолки, стены, низ стен, полы · площади в м², длины в м · отметки в м

## Ведомость отделки помещений (форма 1 прил. А ГОСТ 21.501-2018)

Допущения и предложения на листе. Знак «**» предложено (согласовать): пол пом. 1–8, плинтус пом. 1, 3–6, 8, стены пом. 2, 7, фартук пом. 6. См. лист открытых вопросов (листы 6–11).

| № | Наименование помещения | Потолок | | | Стены и перегородки | | | Низ стен (плинтус) | | | Пол | | Примечание |
|---|---|---|---|---|---|---|---|---|---|---|---|---|---|
| | | Вид отделки | Код цвета | S, м² | Вид отделки | Код цвета | S, м² | Вид отделки | Код цвета | L, м | Вид отделки | S, м² | |
| 1 | Спальня 1<br>17,75 м² | ГКЛ по каркасу П113, отм. +2,500; +2,600; окраска, Tikkurila Anti-Reflex 2, глубокоматовая, 2 слоя, подготовка Q3 | Tikkurila V503 | 17,75 | Окраска, Farrow & Ball Modern Emulsion, матовая, 2 слоя, подготовка Q3<br><br>Акцент — стена А: окраска, Farrow & Ball Modern Emulsion, матовая, 2 слоя, подготовка Q3 | Farrow & Ball No. 241<br><br>Farrow & Ball No. 30 | 25,00<br><br>14,18 | Плинтус МДФ h=80 мм, аналог: МДФ под покраску 80×16 | Farrow & Ball No. 241 | 16,8 | Аналог: инженерная доска, дуб натуральный, масло, 1-полосная, 14/4 мм, на клею; тип 1, отм. ЧП ±0,000 | 17,75 | Н стен 2500 (до потолка); плинтус в цвет: стены |
| 2 | Ванная<br>4,43 м² | ГКЛВ по каркасу П113, отм. +2,389; окраска, Tikkurila Luja 7, матовая, 2 слоя, подготовка Q3 | Tikkurila V503 | 4,43 | Облицовка плиткой, аналог: керамогранит под травертин, матовый, 600×1200×9 мм, клей C2 TE S1, затирка CG2WA | по артикулу | 18,61 | нет | | | Аналог: керамогранит ректифицированный под травертин, матовый, 600×600×9 мм; тип 2, отм. ЧП −0,015 | 4,43 | Н стен 2404 (до потолка); гидроизоляция обмазочная, 2 слоя, с заведением на стены 200 мм (по пирогу пола); тест проливом и акт скрытых работ |
| 3 | Гардеробная<br>1,85 м² | Окраска, Tikkurila Anti-Reflex 2, глубокоматовая, 2 слоя, подготовка Q3 | Tikkurila V503 | 1,85 | Окраска, Tikkurila Harmony, матовая, 2 слоя, подготовка Q3 | Tikkurila V503 | 14,74 | Плинтус МДФ h=80 мм, аналог: МДФ под покраску 80×16 | Tikkurila V503 | 5,3 | Аналог: инженерная доска, дуб натуральный, масло, 1-полосная, 14/4 мм, на клею; тип 1, отм. ЧП ±0,000 | 1,85 | Н стен 2700 (до потолка); плинтус в цвет: стены |
| 4 | Спальня 2<br>12,80 м² | ГКЛ по каркасу П113, отм. +2,500; +2,600; окраска, Tikkurila Anti-Reflex 2, глубокоматовая, 2 слоя, подготовка Q3 | Tikkurila V503 | 12,80 | Окраска, Farrow & Ball Modern Emulsion, матовая, 2 слоя, подготовка Q3<br><br>Акцент — стена А: окраска, Farrow & Ball Modern Emulsion, матовая, 2 слоя, подготовка Q3 | Farrow & Ball No. 241<br><br>Farrow & Ball No. 30 | 22,21<br><br>10,22 | Плинтус МДФ h=80 мм, аналог: МДФ под покраску 80×16 | Farrow & Ball No. 241 | 13,6 | Аналог: инженерная доска, дуб натуральный, масло, 1-полосная, 14/4 мм, на клею; тип 1, отм. ЧП ±0,000 | 12,80 | Н стен 2500 (до потолка); плинтус в цвет: стены |
| 5 | Прихожая<br>7,13 м² | ГКЛ по каркасу П113, отм. +2,620; окраска, Tikkurila Anti-Reflex 2, глубокоматовая, 2 слоя, подготовка Q3 | Tikkurila V503 | 7,13 | Окраска, Farrow & Ball Modern Emulsion, матовая, 2 слоя, подготовка Q3 | Farrow & Ball No. 241 | 21,86 | Плинтус МДФ h=80 мм, аналог: МДФ под покраску 80×16 | Farrow & Ball No. 241 | 7,8 | Аналог: керамогранит ректифицированный под травертин, матовый, 600×1200×9 мм; тип 3, отм. ЧП ±0,000 | 7,13 | Н стен 2620 (до потолка); матовая моющаяся, класс 1 EN 13300 — осознанно вместо полуматовой; плинтус в цвет: стены |
| 6 | Кухня-гостиная<br>29,20 м² | ГКЛ по каркасу П113, отм. +2,500; +2,600; окраска, Tikkurila Anti-Reflex 2, глубокоматовая, 2 слоя, подготовка Q3 | Tikkurila V503 | 29,20 | Окраска, Farrow & Ball Modern Emulsion, матовая, 2 слоя, подготовка Q3<br><br>Акцент — стена А: окраска, Farrow & Ball Modern Emulsion, матовая, 2 слоя, подготовка Q3<br>Фартук кухни (стена В): облицовка керамогранитом, аналог: керамогранит под травертин, матовый, 1200×600×9 мм, клей C2 TE S1, затирка CG2WA | Farrow & Ball No. 241<br><br>Farrow & Ball No. 30<br><br>по артикулу | 35,51<br><br>14,18<br><br>1,87 | Плинтус МДФ h=80 мм, аналог: МДФ под покраску 80×16 | Farrow & Ball No. 241 | 22,2 | Аналог: инженерная доска, дуб натуральный, масло, 1-полосная, 14/4 мм, на клею; тип 1, отм. ЧП ±0,000 | 29,20 | Н стен 2500 (до потолка); матовая моющаяся, класс 1 EN 13300 — осознанно вместо полуматовой; плинтус в цвет: стены |
| 7 | Санузел 2<br>2,29 м² | ГКЛВ по каркасу П113, отм. +2,389; окраска, Tikkurila Luja 7, матовая, 2 слоя, подготовка Q3 | Tikkurila V503 | 2,29 | Облицовка плиткой, аналог: керамогранит под травертин, матовый, 600×1200×9 мм, клей C2 TE S1, затирка CG2WA | по артикулу | 13,10 | нет | | | Аналог: керамогранит ректифицированный под травертин, матовый, 600×600×9 мм; тип 2, отм. ЧП −0,015 | 2,29 | Н стен 2404 (до потолка); гидроизоляция обмазочная, 2 слоя, с заведением на стены 200 мм (по пирогу пола); тест проливом и акт скрытых работ |
| 8 | Коридор<br>3,50 м² | ГКЛ по каркасу П113, отм. +2,620; окраска, Tikkurila Anti-Reflex 2, глубокоматовая, 2 слоя, подготовка Q3 | Tikkurila V503 | 3,50 | Окраска, Farrow & Ball Modern Emulsion, матовая, 2 слоя, подготовка Q3 | Farrow & Ball No. 241 | 14,17 | Плинтус МДФ h=80 мм, аналог: МДФ под покраску 80×16 | Farrow & Ball No. 241 | 4,5 | Аналог: инженерная доска, дуб натуральный, масло, 1-полосная, 14/4 мм, на клею; тип 1, отм. ЧП ±0,000 | 3,50 | Н стен 2620 (до потолка); матовая моющаяся, класс 1 EN 13300 — осознанно вместо полуматовой; плинтус в цвет: стены |
| | **Итого** | | | **78,95** | | | **205,64** | | | **70,3** | | **78,95** | |

### Примечания

1. Площади поверхностей — по чистым граням стен до отделки: стены = периметр × высоту от чистого пола помещения до низа потолка минус проёмы (облицовка плиткой — до верха облицовки); плинтус = периметр минус дверные проёмы; пол и потолок — по площади помещения. Количество плиток по раскладке. Площади помещений — с учётом всех частей помещения; откосы в площадь стен не входят.
2. Акцентные стены и фартук — отдельными строками, их площадь вычтена из основной отделки стен помещения; фартук — над нижними модулями кухни от столешницы до низа навесных шкафов, где шкафов нет — на 600 мм.
3. Плинтус — длина по периметру за вычетом дверных проёмов; примыкания к наличникам и встроенной мебели — по развёрткам.
4. Формат плитки — Ш×В×Т (ширина × высота в положении укладки × толщина), мм; на полу — вдоль стен А/В × вдоль стен Б/Г.
5. Коды цвета — по веерам производителей; колеровка каждой краски одной партией, проверка выкраса при свете D65 и при лампах проекта.
6. Уровни подготовки Q1–Q4 — система Knauf, не норма ГОСТ/СП; допуски поверхностей — по СП 71.13330.2017 (действующая редакция).
7. «Каналог:» — изделие задано характеристиками, марку и артикул согласовать с заказчиком до закупки.
8. Сводка площадей по материалам, м²: потолок — Tikkurila V503 Anti-Reflex 2 — 72,23; потолок — Tikkurila V503 Luja 7 — 6,72; стены — Farrow & Ball No. 241 Modern Emulsion — 118,75; стены — Farrow & Ball No. 30 Modern Emulsion — 38,58; стены — облицовка плиткой 600×1200×9 мм — 31,71; стены — Tikkurila V503 Harmony — 14,74; фартук — облицовка керамогранитом 1200×600×9 мм — 1,87.

| Изм. | Кол.уч | Лист | № док. | Подп. | Дата |
|---|---|---|---|---|---|
| Разраб. | | Кырпан А.С. | | | 05.10.26 |
| Пров. | | | | | |
| ГИП | | | | | |
| | | | | | |
| Н. контр. | | | | | |
| Утв. | | | | | |

**ГД-2026-003-АИ**

Трёхкомнатная квартира

Общая площадь 78,95* м² · * размеры со скана, не замерены (реестр — п. 6–11, К-13)

Дизайн-проект интерьера трёхкомнатной квартиры

| Стадия | Лист | Листов |
|---|---|---|
| РП | 51 | 94 |

**Ведомость отделки помещений**

М 6/м

Кырпан Александр Сергеевич

выпуск 05.10.2026 № 6add39ab8d · стр. 60 из 137

# Колерная карта

Цвета и материалы по помещениям · палитра проекта · выкрасы на согласование

## Колерная карта по помещениям

| Помещение | Поверхность | Образец | Поз. | Система и код цвета | Производитель, линейка / материал, артикул | Блеск | Класс EN 13300 | LRV | Площадь |
|---|---|---|---|---|---|---|---|---|---|
| **1. Спальня 1** 17,75 м² | стены | | K1 | Farrow & Ball No. 241 | Farrow & Ball · Modern Emulsion | матовая | 1 | 67 | 25,0 м² |
| | акцент А | | K2 | Farrow & Ball No. 30 | Farrow & Ball · Modern Emulsion | матовая | 1 | 7 | 14,2 м² |
| | потолок | | K3 | Tikkurila V503 | Tikkurila · Anti-Reflex 2 | глубокомат. | 2 | 86 | 17,8 м² |
| | пол | | KM1 | по образцу | инженерная доска · аналог по хар. | | | | 17,8 м² |
| | плинтус | | K4 | Farrow & Ball No. 241 | МДФ · в цвет Farrow & Ball | | | 67 | 16,8 м |
| **2. Ванная** 4,43 м² | стены | | KM2 | по образцу | плитка · аналог по хар. | | | | 18,6 м² |
| | потолок | | K5 | Tikkurila V503 | Tikkurila · Luja 7 | матовая | 1 | 86 | 4,4 м² |
| | пол | | KM3 | по образцу | керамогранит · аналог по хар. | | | | 4,4 м² |
| **3. Гардеробная** 1,85 м² | стены | | K6 | Tikkurila V503 | Tikkurila · Harmony | матовая | 1 | 86 | 14,7 м² |
| | потолок | | K3 | Tikkurila V503 | Tikkurila · Anti-Reflex 2 | глубокомат. | 2 | 86 | 1,9 м² |
| | пол | | KM1 | по образцу | инженерная доска · аналог по хар. | | | | 1,9 м² |
| | плинтус | | K7 | Tikkurila V503 | МДФ · в цвет Tikkurila | | | 86 | 5,3 м |
| **4. Спальня 2** 12,8 м² | стены | | K1 | Farrow & Ball No. 241 | Farrow & Ball · Modern Emulsion | матовая | 1 | 67 | 22,2 м² |
| | акцент А | | K2 | Farrow & Ball No. 30 | Farrow & Ball · Modern Emulsion | матовая | 1 | 7 | 10,2 м² |
| | потолок | | K3 | Tikkurila V503 | Tikkurila · Anti-Reflex 2 | глубокомат. | 2 | 86 | 12,8 м² |
| | пол | | KM1 | по образцу | инженерная доска · аналог по хар. | | | | 12,8 м² |
| | плинтус | | K4 | Farrow & Ball No. 241 | МДФ · в цвет Farrow & Ball | | | 67 | 13,6 м |
| **5. Прихожая** 7,13 м² | стены | | K1 | Farrow & Ball No. 241 | Farrow & Ball · Modern Emulsion | матовая | 1 | 67 | 21,9 м² |
| | потолок | | K3 | Tikkurila V503 | Tikkurila · Anti-Reflex 2 | глубокомат. | 2 | 86 | 7,1 м² |
| | пол | | KM4 | по образцу | керамогранит · аналог по хар. | | | | 7,1 м² |
| | плинтус | | K4 | Farrow & Ball No. 241 | МДФ · в цвет Farrow & Ball | | | 67 | 7,8 м |
| **6. Кухня-гостиная** 29,2 м² | стены | | K1 | Farrow & Ball No. 241 | Farrow & Ball · Modern Emulsion | матовая | 1 | 67 | 35,5 м² |
| | акцент А | | K2 | Farrow & Ball No. 30 | Farrow & Ball · Modern Emulsion | матовая | 1 | 7 | 14,2 м² |
| | потолок | | K3 | Tikkurila V503 | Tikkurila · Anti-Reflex 2 | глубокомат. | 2 | 86 | 29,2 м² |
| | пол | | KM1 | по образцу | инженерная доска · аналог по хар. | | | | 29,2 м² |
| | плинтус | | K4 | Farrow & Ball No. 241 | МДФ · в цвет Farrow & Ball | | | 67 | 22,2 м |
| | фартук | | KM5 | по образцу | керамогранит · аналог по хар. | | | | 1,9 м² |
| **7. Санузел 2** 2,29 м² | стены | | KM2 | по образцу | плитка · аналог по хар. | | | | 13,1 м² |
| | потолок | | K5 | Tikkurila V503 | Tikkurila · Luja 7 | матовая | 1 | 86 | 2,3 м² |
| | пол | | KM3 | по образцу | керамогранит · аналог по хар. | | | | 2,3 м² |
| **8. Коридор** 3,5 м² | стены | | K1 | Farrow & Ball No. 241 | Farrow & Ball · Modern Emulsion | матовая | 1 | 67 | 14,2 м² |
| | потолок | | K3 | Tikkurila V503 | Tikkurila · Anti-Reflex 2 | глубокомат. | 2 | 86 | 3,5 м² |
| | пол | | KM1 | по образцу | инженерная доска · аналог по хар. | | | | 3,5 м² |
| | плинтус | | K4 | Farrow & Ball No. 241 | МДФ · в цвет Farrow & Ball | | | 67 | 4,5 м |

## Перечень выкрасов на согласование

| № | Код | Бренд / веер | Пом. / стена | Подложка | Формат | Статус |
|---|---|---|---|---|---|---|
| 1 | No. 241 | Farrow & Ball | 1, 4, 5, 6, 8 | ГКЛ, загрунтованный под эту краску; МДФ, загрунтованный под эмаль | 600×1000; 300×600 | к выполнению |
| 2 | No. 30 | Farrow & Ball | 1 А, 4 А, 6 А | ГКЛ, загрунтованный под эту краску | 600×1000 | к выполнению |
| 3 | V503 | Tikkurila | 1, 2, 3, 4, 5, 6, 7, 8 | ГКЛ, загрунтованный под эту краску; МДФ, загрунтованный под эмаль | 600×1000; 300×600 | к выполнению |

## Примечания

1. Цвет утверждается только по выкрасу на объекте: формат от А3 до 1000×1000 мм на загрунтованном ГКЛ, в 2 слоя (как на стене), не на белой шпаклёвке; смотреть днём и при свете проекта своего помещения, рядом с образцами пола и фасадов. Подпись на обороте: код, бренд и веер, дата.
2. Колеровка машинная в колеровочном центре бренда; каждый код — за один проход, одной партией на весь объём. Колеровщику передаётся только система и код утверждённого веера; плашки и HEX на листе — ориентир, печать не является эталоном цвета.
3. Класс мокрого истирания — EN 13300 (ISO 11998); блеск — по ГОСТ 31975 (ISO 2813), геометрия 60°. LRV — пересчёт координаты L* каталога производителя (Y = ((L*+16)/116)³); «≈» — расчёт по HEX, справочно.
4. Площади поверхностей — тем же способом и с теми же цифрами, что в ведомости отделки (способ счёта — в общих указаниях); объём краски к заказу, фасовка и материалы КМ — в спецификации отделочных материалов.
5. Перечень выкрасов составлен по кодам колерной карты; к основному тону стен добавить на выкрас 2 соседних тона того же веера (светлее и темнее), статус отмечать в графе «Статус» при согласовании.

Допущения и предложения на листе. Знак «*» предложено (согласовать): пол пом. 1–8, плинтус пом. 1, 3–6, 8, стены пом. 2, 7, фартук пом. 6. См. лист открытых вопросов (листы 6–11).

## Схема квартиры: цвет стен и акценты (б/м)

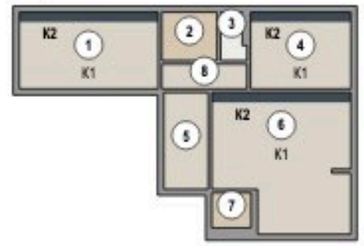


## Схема палитры проекта

Стиль: Современный (контемпорари) · схема: аналоговая

| основной | основной | второстепенный | акцентный |
|---|---|---|---|
| **Tikkurila V503** | **Farrow & Ball No. 241** | **Tikkurila H487** | **Farrow & Ball No. 30** |
| Winter<br>LRV 86<br>потолок 1,2,3,4,5,6,7,8; стены 3; плинтус 3; текстиль/декор 1,4,6 | Skimming Stone<br>LRV 67<br>стены 1,4,5,6,8; плинтус 1,4,5,6,8 | Pumice<br>LRV 57<br>текстиль/декор 1,4,6 | Hague Blue<br>LRV 7<br>акцент 1,4,6; текстиль/декор 1,4,6 |

План 60/30/10

| 60% | 30% | 10% |
|---|---|---|

Окраска, факт — по площади стен, акцентов, потолков

| 85% | 15% |
|---|---|

окрашено всего 251 м²; второстепенный тон несут мебель и текстиль

**Текстиль и декор в цветах вне палитры проекта**

- NCS S 3005-Y20R тёплый тауп-серый — пом. 1 (Т3)
- Farrow & Ball No. 229 Elephant's Breath — пом. 4 (Т10)
- Tikkurila V484 Driftwood — пом. 4 (Т9), 6 (Т15, Т16, Т19)
- Farrow & Ball No. 47 Green Smoke — пом. 4 (Т11)

## Условные обозначения

- K1 — Farrow & Ball No. 241 · Skimming Stone · Modern Emulsion · матовая · кл. 1
- K2 — Farrow & Ball No. 30 · Hague Blue · Modern Emulsion · матовая · кл. 1
- K3 — Tikkurila V503 · Winter · Anti-Reflex 2 · глубокомат. · кл. 2
- K4 — Farrow & Ball No. 241 · Skimming Stone · МДФ
- K5 — Tikkurila V503 · Winter · Luja 7 · матовая · кл. 1
- K6 — Tikkurila V503 · Winter · Harmony · матовая · кл. 1
- K7 — Tikkurila V503 · Winter · МДФ
- дерево (доска, паркет, ламинат) — рисунок досок
- керамогранит, плитка, камень — сетка швов по формату
- KM1 — аналог: инженерная доска, дуб натуральный, масло, 1-полосная, 14/4 мм
- KM2 — плитка · аналог: керамогранит под травертин, матовый, 600×1200×9 мм
- KM3 — аналог: керамогранит ректифицированный под травертин, матовый, 600×600×9 мм
- KM4 — аналог: керамогранит ректифицированный под травертин, матовый, 600×1200×9 мм
- KM5 — аналог: керамогранит под травертин, матовый, 1200×600×9 мм

К — позиция окраски (код + продукт + блеск), КМ — позиция материала, тон КМ — по описанию артикула, эталон — образец материала; ≈ LRV — расчёт по HEX, справочно

| Изм. | Кол.уч | Лист | № док. | Подп. | Дата |
|---|---|---|---|---|---|
| Разраб. | | Кырпан А.С. | | | 05.10.26 |
| Пров. | | | | | |
| ГИП | | | | | |
| | | | | | |
| Н. контр. | | | | | |
| Утв. | | | | | |

**ГД-2026-003-АИ**

Трёхкомнатная квартира

Общая площадь 78,95* м² · * размеры со скана, не замерены (реестр — п. 6–11, К-13)

| Дизайн-проект интерьера трёхкомнатной квартиры | Стадия | Лист | Листов |
|---|---|---|---|
| | РП | 52 | 94 |

**Колерная карта**

М б/м

Кырпан Александр Сергеевич

выпуск 05.10.2026 · 6add39ab8d · стр. 61 из 137

# Спецификация отделочных материалов

ПРЕДВАРИТЕЛЬНО · не для производства работ · открыто пунктов: 31 (реестр — л. 6–11)

Форма 1 по ГОСТ 21.110-2013 · количества — из геометрии проекта, с запасом

| Поз. | Наименование и техническая характеристика | Тип, марка, обозначение документа | Код продукции | Поставщик | Ед. изм. | Кол. | Масса 1 ед., кг | Примечание |
|---|---|---|---|---|---|---|---|---|
| | **Лакокрасочные материалы** | | | | | | | |
| 1 | Краска интерьерная водно-дисперсионная акриловая для стен, матовая, класс мокрого истирания 1 по EN 13300, база A; цвет Farrow & Ball No. 241 «Skimming Stone», колеровка машинная | Farrow & Ball Modern Emulsion | | Farrow & Ball | л | 32,5 | | поз. К1 колерной карты; пом. 1, 4, 5, 6, 8; S = 118,8 м² × 2 сл. × 0,12 л/м² = 28,5 л, +10 % и 0,5 л на подкраску → ≥ 31,9 л; тара 6 × 5 л + 1 × 2,5 л |
| 2 | Краска интерьерная водно-дисперсионная акриловая для акцентных стен, матовая, класс мокрого истирания 1 по EN 13300, база C; цвет Farrow & Ball No. 30 «Hague Blue», колеровка машинная | Farrow & Ball Modern Emulsion | | Farrow & Ball | л | 12,5 | | поз. К2 колерной карты; пом. 1, 4, 6; S = 38,6 м² × 2 сл. × 0,12 л/м² = 9,3 л, +10 % и 0,5 л на подкраску → ≥ 10,7 л; тара 2 × 5 л + 1 × 2,5 л |
| 3 | Краска интерьерная водно-дисперсионная акриловая для потолков, глубокоматовая, класс мокрого истирания 2 по EN 13300, база A; цвет Tikkurila V503 «Winter», колеровка машинная | Tikkurila Anti-Reflex 2 | | Tikkurila | л | 19,8 | | поз. К3 колерной карты; пом. 1, 3, 4, 5, 6, 8; S = 72,2 м² × 2 сл. × 0,12 л/м² = 17,3 л, +10 % и 0,5 л на подкраску → ≥ 19,6 л; тара 2 × 9 л + 2 × 0,9 л |
| 4 | Краска интерьерная водно-дисперсионная акриловая для потолков, матовая, класс мокрого истирания 1 по EN 13300, база A; цвет Tikkurila V503 «Winter», колеровка машинная | Tikkurila Luja 7 | | Tikkurila | л | 2,7 | | поз. К5 колерной карты; пом. 2, 7; S = 6,7 м² × 2 сл. × 0,12 л/м² = 1,6 л, +10 % и 0,5 л на подкраску → ≥ 2,3 л; тара 1 × 2,7 л |
| 5 | Краска интерьерная водно-дисперсионная акриловая для стен, матовая, класс мокрого истирания 1 по EN 13300, база A; цвет Tikkurila V503 «Winter», колеровка машинная | Tikkurila Harmony | | Tikkurila | л | 4,5 | | поз. К6 колерной карты; пом. 3; S = 14,7 м² × 2 сл. × 0,12 л/м² = 3,5 л, +10 % и 0,5 л на подкраску → ≥ 4,4 л; тара 1 × 2,7 л + 2 × 0,9 л |
| 6 | Краска для МДФ и дерева в цвет Farrow & Ball No. 241 «Skimming Stone» — окраска плинтуса; блеск не ниже блеска стен | марка не задана | | | л | 1,7 | | поз. К4; пом. 1, 4, 5, 6, 8; L = 65,1 м, S = 6,2 м² × 2 сл. × 0,12 л/м² + 10 %; продукт подобрать в веере Farrow & Ball |
| 7 | Краска для МДФ и дерева в цвет Tikkurila V503 «Winter» — окраска плинтуса; блеск не ниже блеска стен | марка не задана | | | л | 0,5 | | поз. К7; пом. 3; L = 5,3 м, S = 0,5 м² × 2 сл. × 0,12 л/м² + 10 %; продукт подобрать в веере Tikkurila |
| 8 | Грунтовка акриловая под окраску стен и потолков — из системы производителя краски | по системе краски | | | м² | 252 | | площадь окраски стен, акцентов и потолков; 1 слой перед окраской; расход — по ТУ грунтовки |
| | **Плитка и керамогранит** | | | | | | | |
| 9 | Керамогранит под травертин, 600×600×9 мм, ректификат, водопоглощение 0,1 % (BIa), противоскольжение R10, PEI IV | аналог по характеристикам | | | м² | 9,72 | | шов 2 мм; Ванная, пол; Санузел 2, пол; по раскладке 24 шт (S = 6,72 м²), с запасом 27 шт |
| 10 | Керамогранит под травертин, 600×1200×9 мм, ректификат, водопоглощение 0,1 % | аналог по характеристикам | | | м² | 54 | | шов 2 мм; Ванная, стены А–Г; Ванная, короб инсталляции; Санузел 2, стены А–Г; Санузел 2, короб инсталляции; по раскладке 65 шт (S = 33,26 м²), с запасом 75 шт |
| 11 | Керамогранит ректифицированный под травертин, матовый, 600×1200×9 мм, водопоглощение 0,1 % (BIa), противоскольжение R10, PEI IV | аналог по характеристикам | | | м² | 10,08 | | шов 2 мм; Прихожая, пол; по раскладке 12 шт (S = 7,13 м²), с запасом 14 шт |
| 12 | Керамогранит под травертин, матовый, 1200×600×9 мм, ректификат, водопоглощение 0,1 % (BIa) | аналог по характеристикам | | | м² | 3,60 | | шов 2 мм; Кухня-гостиная, фартук (ст. В); по раскладке 4 шт (S = 1,87 м²), с запасом 5 шт |
| | **Напольные покрытия** | | | | | | | |
| 13 | Инженерная доска, дуб натуральный, масло, 1-полосная, 14/4 мм, эмиссия E1, укладка на клей | аналог по характеристикам | | | м² | 69,7 | | пом. 1, 3, 4, 6, 8; S = 65,10 м² + 7 % (прямая укладка); к заказу — кратно упаковке |
| 14 | Клей для паркета и инженерной доски, эластичный (СМП / полиуретановый) | по рекомендации производителя доски | | | м² | 66 | | площадь приклейки; расход и шпатель — по ТУ клея |
| | **Погонажные изделия** | | | | | | | |
| 15 | Плинтус МДФ под покраску 80×16, крепление к стене, окраска в цвет Farrow & Ball No. 241 | аналог по характеристикам | | | м | 78 | | пом. 1, 3, 4, 5, 6, 8; L = 70,3 м (периметр без дверных проёмов) + 10 % на подрезку; в штуках — по длине планки |
| | **Смеси и материалы для облицовки** | | | | | | | |
| 16 | Затирка для швов плитки, класс CG2WA по EN 13888 | Mapei Ultracolor Plus 132 | | Mapei | кг | 3,8 | | по раскладке (a+b)/(a·b) × шов × t × 1,6 + 10 %; в т. ч. 0,7 кг — позиции раскладки без марки |
| 17 | Клей плиточный C2 TE S1 по EN 12004, слой 5 мм | Ceresit CM 17 | | Ceresit | кг | 385 | | 16 меш. по 25 кг; 1,5 кг/м² на 1 мм слоя + 10 %; в т. ч. 73 кг — позиции раскладки без марки |
| 18 | Гидроизоляция обмазочная мокрых зон: пол, стены по периметру, зоны замачивания; 2 слоя с армирующей лентой в углах | аналог по характеристикам | | | м² | 20 | | площадь по листу раскладки плитки + 10 %; расход смеси — по ТУ |
| 19 | Лента демпферная по периметру пола из плитки | аналог по характеристикам | | | м | 22,4 | | периметр без дверных проёмов + 10 % |

## Примечания

1. Количества — из геометрии проекта: площади поверхностей по чистым граням стен до отделки (те же, что в ведомости отделки и колерной карте), плитка, клей и затирка — по раскладке плиточника; в графе «Кол.» — к заказу, с запасом.
2. Краска: расход 0,12 л/м² на слой в 2 слоя, если по ТУ не задан иной; запас 10 % и 0,5 л на подкраску каждого кода. Один код — одна партия, колеровка машинная в колеровочном центре бренда; в заказ — только после утверждения выкраса (колерная карта). Фасовка — по каталогу бренда на дату выпуска; к заказу — не меньше расчётного объёма.
3. «Аналог по характеристикам» — допускается изделие другого производителя с характеристиками не ниже указанных, по согласованию с автором проекта.
4. Графы «Код продукции» и «Масса 1 ед.» не заполнены: коды по классификатору продукции не присвоены, масса единицы до 25 кг (ГОСТ 21.110-2013).
5. Грунтовка и клей для доски указаны площадью обработки; объём — по ТУ выбранного продукта.

Допущения и предложения на листе. Основа листа: размеры сняты со скана плана заказчика по размерным цепочкам, контрольный обмер на объекте не выполнялся (К-13); высота потолка 2700 мм принята: на плане заказчика не указана (К-11); толщины стен приняты: наружные 250 мм, перегородки 150 мм (на плане 85–190 мм) (К-13); разрешённая мощность 15 кВт принята по типовой квартире, технических условий нет (К-14); утолщение стены 190 × 1360 мм и элемент 1470 × 160 мм плана заказчика не определены (К-12); ниши санузла 2 закрыты перегородкой и фальш-стеной: проектное решение, на плане заказчика ниша у входа открыта (К-18); несущие стены не определены: до технического заключения все существующие стены считаются несущими (К-20); окна существующие и сохраняются; подоконная доска и глубина откосов не заданы — приняты, не замерены (К-27). Знак «**» — предложение проектировщика, заказчиком не утверждено (согласовать с заказчиком): ИЗ-2, К-2, К-23: пол пом. 2, 7 — пирог пола: стяжка 33 мм и обмазочная гидроизоляция добавлены разработчиком проекта; артикул изделия не выбран: позиция описана характеристиками («аналог по характеристикам»), артикул выбирается при закупке; К-2, К-23: стены пом. 2, 7 — артикул изделия не выбран: позиция описана характеристиками («аналог по характеристикам»), артикул выбирается при закупке; К-23: пол пом. 1, 3–6, 8, плинтус пом. 1, 3–6, 8, фартук пом. 6 — артикул изделия не выбран: позиция описана характеристиками («аналог по характеристикам»), артикул выбирается при закупке. См. лист открытых вопросов (лист 6, записи К-2, К-11; лист 7, записи К-12–К-14, К-18, К-20; лист 8, записи К-23, К-27; лист 9, запись ИЗ-2); по листу — К-23.

| Изм. | Кол.уч | Лист | № док. | Подп. | Дата |
|---|---|---|---|---|---|
| Разраб. | | Кырпан А.С. | | | 05.10.26 |
| Пров. | | | | | |
| ГИП | | | | | |
| | | | | | |
| Н. контр. | | | | | |
| Утв. | | | | | |

**ГД-2026-003-АИ**

Трёхкомнатная квартира

Общая площадь 78,95* м² · * размеры со скана, не замерены (реестр — л. 6–11, К-13)

| Дизайн-проект интерьера трёхкомнатной квартиры | Стадия | Лист | Листов |
|---|---|---|---|
| | РП | 53 | 94 |
| **Спецификация отделочных материалов** М 6/м | **Кырпан Александр Сергеевич** | | |

выпуск 05.10.2026 · 6add39ab8d · стр. 62 из 137

# Концепция декора и визуализации

Современный (контемпорари) · warm contemporary · визуализации, палитра, материалы, ключевые предметы

**В1. Вид сверху (3D): планировка с мебелью, текстилем и декором**

Расстановка — по плану мебели (лист 26); шторы, ковры, картины и растения — по плану текстиля и декора (лист 55).

**В24. Кухня-гостиная (пом. 6)**

шторы Т13, Т14, Т15 · ковёр Т16 · картина ДК6 · растение ДК7 · подушки, пледы Т17, Т18, Т19

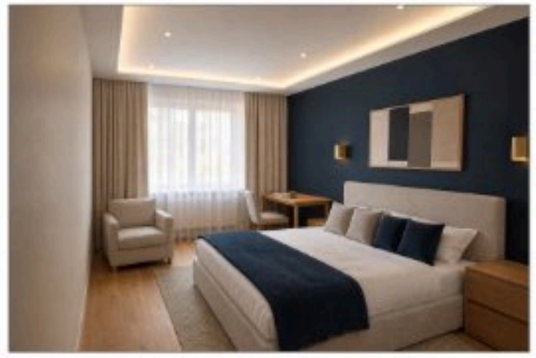

**В14. Спальня 1 (пом. 1)**

шторы Т1, Т2 · ковёр Т3 · картина ДК1 · подушки, пледы Т4, Т5, Т6

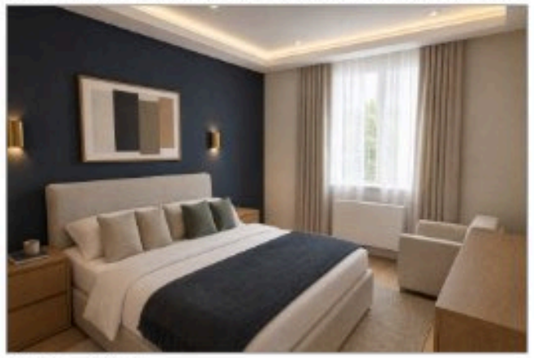

**В17. Спальня 2 (пом. 4)**

шторы Т7, Т8 · ковёр Т9 · картина ДК3 · зеркало ДК4 · подушки, пледы Т10, Т11, Т12

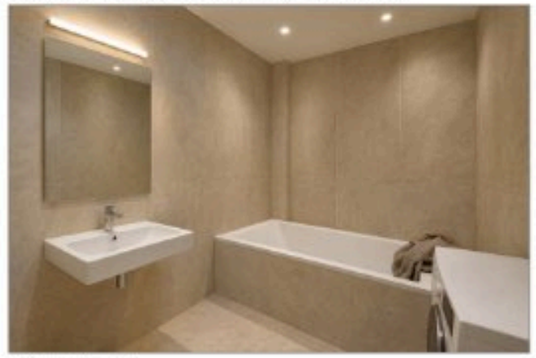

**В8. Ванная (пом. 2)**

зеркало ДК2

## Материалы и фактуры

**Дуб натуральный**
пол: пом. 1, 3, 4, 6, 8; рамы ДК1, ДК3

**Травертин (керамогранит)**
пол и стены санузлов, фартук: пом. 2, 5, 6, 7

**Букле**
подушки: Т10, Т17

**Лён**
портьеры, подушки, римская штора: Т1, Т4, Т7, Т13, Т15

**Бронза и чёрный металл**
рамы ДК4, ДК5 — чёрный; фурнитура, светильники — бронза

## Ключевые предметы

- Диван М2 2600×1000 — кухня-гостиная; подушки и плед Т17, Т18, Т19
- Кровати С1, С7 — над изголовьем картины ДК1, ДК3; текстиль Т4, Т5, Т6, Т10, Т11, Т12
- Ковры Т3, Т9, Т16 — шерсть, на противоскользящей подложке
- Картины ДК1, ДК3, ДК6 — центр на высоте 1550–1650 мм
- Зеркала в рост ДК4, ДК5; над умывальниками ДК2, ДК9
- Шторы-волна Т1, Т7, Т13 (Tikkurila H487), тюль Т2, Т8, Т14 (Tikkurila V503) — в нишах потолка
- Растение ДК7, ваза ДК8

## Настроение

Warm contemporary: потолки V503, стены Skimming Stone No. 241, грейж H487 в текстиле, один глубокий акцент Hague Blue No. 30 (изголовья спален, ТВ-стена). Настроение стиля: актуальность, комфорт, мягкая геометрия, контраст фактур, открытость, уверенность. Свет тёплый, 2700–3000 К.

## Примечания

1. Визуализации — образ интерьера. Изделия, размеры, высоты подвеса и привязки — по чертежам (план текстиля и декора — лист 55; шторы и карнизы — лист 56; ведомость текстиля — лист 57; ведомость декора и развеска — лист 58); при расхождении действуют чертежи и ведомости.
2. Коды цвета — ориентир подбора по веерам производителей; ткань утверждается по образцу при дневном свете и при свете проекта 2700–3000 К.
3. Мелкий стайлинг на визуализациях (книги, посуда, свечи) в ведомости не входит и поставляется заказчиком по желанию.

## Палитра 60/30/10 и цвета текстиля

- Tikkurila V503 (Winter), LRV 86 — 60 % база — Т2, Т8, Т14
- Tikkurila H487 (Pumice), LRV 57 — 30 % второй цвет — Т1, Т4, Т7, Т13, Т17
- NCS S 3005-Y20R (тёплый тауп-серый), LRV 44 — текстиль — Т3
- Farrow & Ball No. 229 (Elephant's Breath), LRV 52 — текстиль — Т10
- Farrow & Ball No. 241 (Skimming Stone), LRV 67 — 60 % база
- Farrow & Ball No. 30 (Hague Blue), LRV 7 — 10 % акцент — Т5, Т6, Т12, Т18
- Tikkurila V484 (Driftwood), LRV 49 — текстиль — Т9, Т15, Т16, Т19
- Farrow & Ball No. 47 (Green Smoke), LRV 19 — акцент текстиля — Т11

**Допущения и предложения на листе**

Основа листа: размеры сняты со скана плана заказчика по размерным цепочкам, контрольный обмер на объекте не выполнялся (К-13); высота потолка 2700 мм принята: на плане заказчика не указана (К-11); толщины стен приняты: наружные 250 мм, перегородки 150 мм (на плане 85–190 мм) (К-13); разрешённая мощность 15 кВт принята по типовой квартире, технических условий нет (К-14); утолщение стены 190 × 1360 мм и элемент 1470 × 160 мм плана заказчика не определены (К-12); ниши санузла 2 закрыты перегородкой и фальш-стенкой: проектное решение, на плане заказчика ниша у входа открыта (К-18); несущие стены не определены: до технического заключения все существующие стены считаются несущими (К-20); окна существующие и сохраняются; подоконная доска и глубина откосов не заданы — приняты, не замерены (К-27).
См. лист открытых вопросов (лист 6, запись К-11; лист 7, записи К-12–К-14, К-18, К-20; лист 8, запись К-27).

| | | | | | | | |
|---|---|---|---|---|---|---|---|
| | | | | | | **ГД-2026-003-АИ** | |
| | | | | | | Трёхкомнатная квартира | |
| Изм. | Кол.уч | Лист | № док. | Подп. | Дата | Общая площадь 78,95* м² · * размеры со скана, не замерены (реестр — л. 6–11, К-13) | |
| Разраб. | | Кырпан А.С. | | | 05.10.26 | Дизайн-проект интерьера трёхкомнатной квартиры | Стадия: РП; Лист: 54; Листов: 94 |
| Пров. | | | | | | | |
| ГИП | | | | | | | |
| Н. контр. | | | | | | **Концепция декора и визуализации** М 6/м | Кырпан Александр Сергеевич |
| Утв. | | | | | | | |

выпуск 05.10.2026 · 6add39ab8d · стр. 63 из 137

# План текстиля и декора

Шторы и карнизы, ковры, картины и зеркала, растения · размеры в мм от чистовых стен и чистого пола · марки — по ведомостям

ПРЕДВАРИТЕЛЬНО · не для производства работ · открыто пунктов: 31 (реестр — л. 6–11)

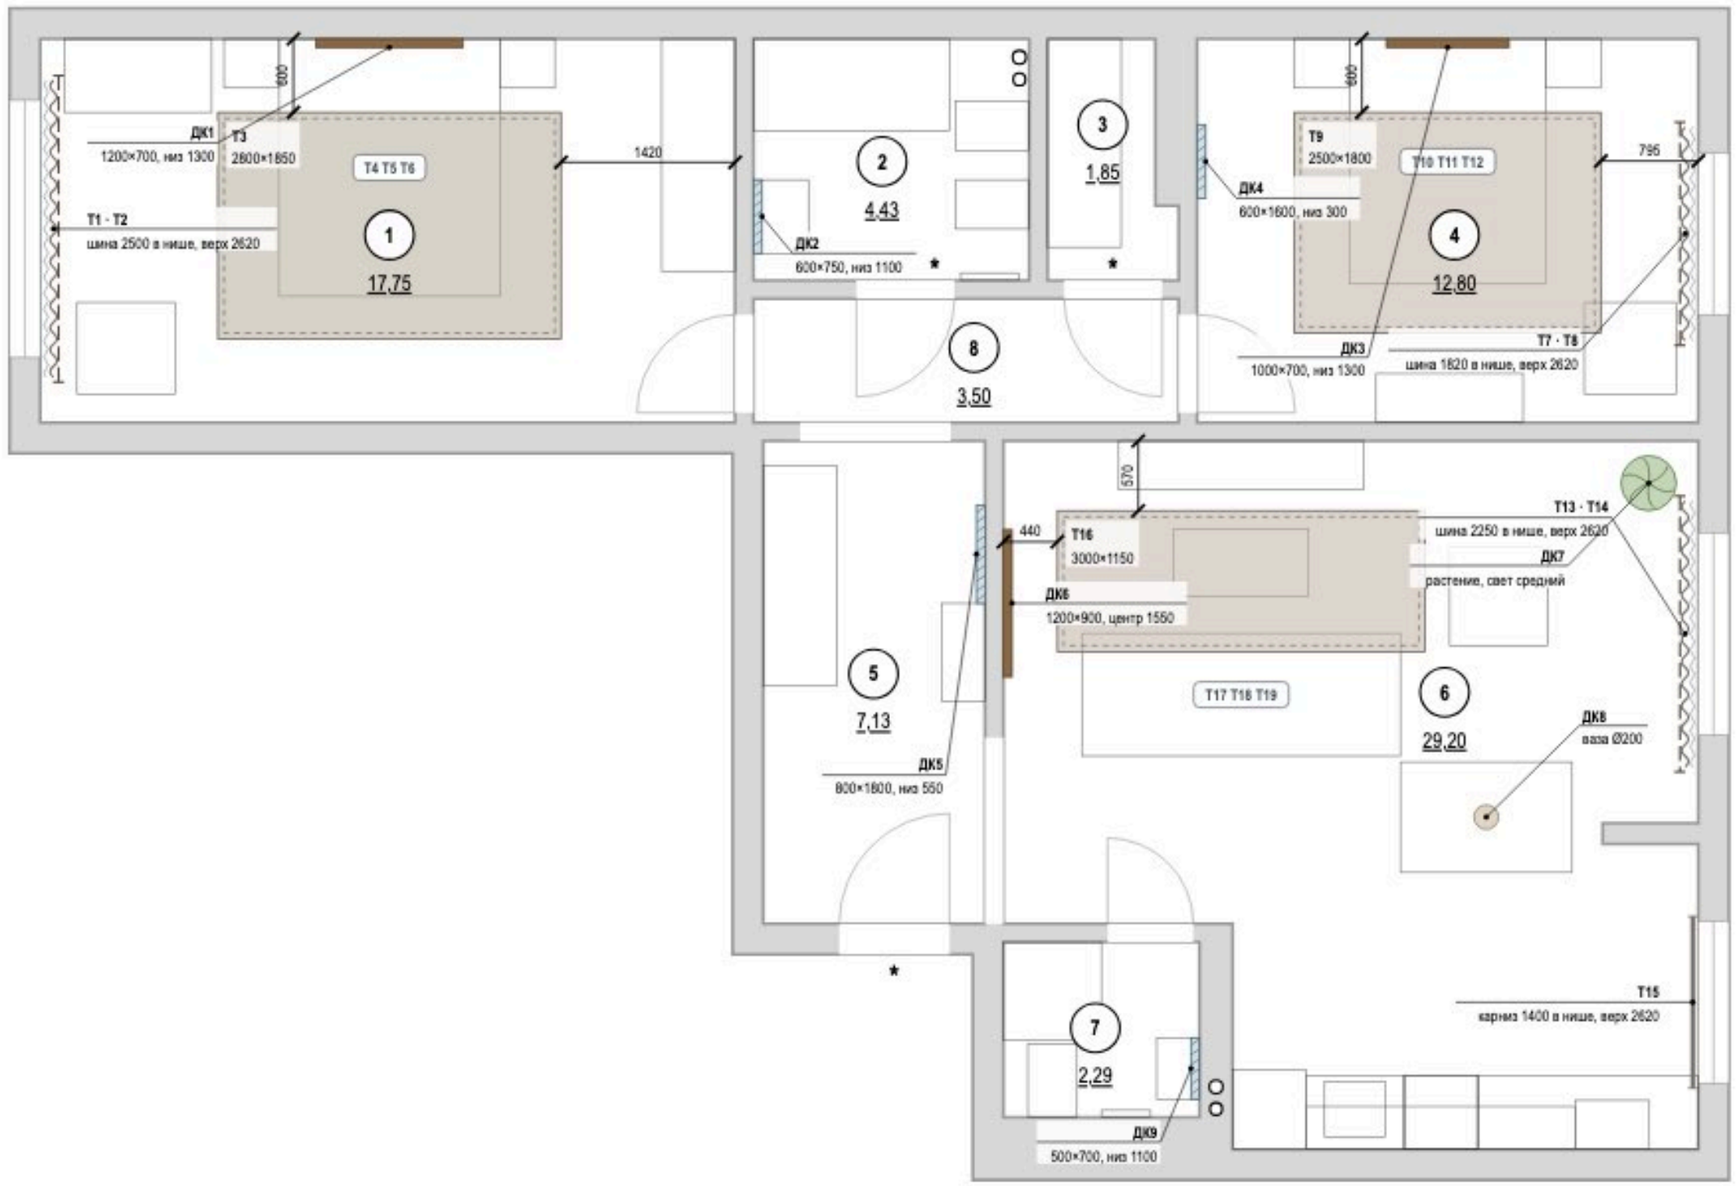


## Условные обозначения

- ковёр — габарит в масштабе, цвет изделия
- шина или карниз штор (выше плоскости разреза)
- портьеры (штора-волна)
- тюль (на плане — волнистая линия)
- римская или рулонная штора в проёме
- картина на стене — ширина в масштабе
- зеркало на стене — ширина в масштабе
- растение в кашпо — диаметр в масштабе
- ваза, настольный декор
- подушки, пледы — марки на мебели
- привязка от чистовой стены, мм
- (1) номер помещения, площадь м²
- стены (подложка обмера)
- ★ «*» — принято, не замерено и не подтверждено

Т1, ДК1 — марки по ведомостям текстиля и декора

**Экспликация помещений**

лист 21 · на плане — номера в марках

## Окна: шина → полотно, мм

| Поз. | Шина | Верх шины | Полотно, низ |
|---|---|---|---|
| Т1, Т2 | 2500 | 2620, ниша | 2610, низ 10 |
| Т7, Т8 | 1820 | 2620, ниша | 2610, низ 10 |
| Т13, Т14 | 2250 | 2620, ниша | 2610, низ 10 |
| Т15 | 1400 | 2620, ниша | 1620, низ 1000 |

## Развеска: высоты от пола, мм

| Поз. | Пом. | Ш×В | Центр | Низ | Стена |
|---|---|---|---|---|---|
| ДК1 | 1 | 1200×700 | 1650 | 1300 | А |
| ДК2 | 2 | 600×750 | 1475 | 1100 | Г |
| ДК3 | 4 | 1000×700 | 1650 | 1300 | А |
| ДК4 | 4 | 600×1600 | 1100 | 300 | Г |
| ДК5 | 5 | 800×1800 | 1450 | 550 | Б |
| ДК6 | 6 | 1200×900 | 1550 | 1100 | Г |
| ДК9 | 7 | 500×700 | 1450 | 1100 | Б |

## Примечания

Допущения и предложения на листе. Знак «*» принято (замерить): Ст К1-1, Ст В1-1, Ст К1-2, Ст В1-2. См. лист открытых вопросов (листы 6–11).

1. Размеры — в мм. Отступы ковров — от чистовых стен; высоты картин и зеркал — от чистого пола до центра или низа рамы.
2. Шторы — на шинах в нишах потолка (ниша — план потолков, лист 44); закладная под шину — до обшивки ГКЛ. Схемы окон, длины полотен и сборка — лист 56.
3. Картины и зеркала массой более 5 кг — на анкеры по основанию, нагрузка крепежа не меньше двойной массы изделия; на ГКЛ — только по закладной. Декор не перекрывает розетки и выключатели.
4. Ковры на гладком полу — на противоскользящей подложке.
5. Мебель — по плану расстановки мебели (лист 26); ведомость текстиля — лист 57, ведомость декора и схемы развески — лист 58.
6. Знак «*» у проёма — допущение: положение проёма не замерено (дверь пом. 5, стена В; дверь пом. 8, стена А (2 шт.)); размер напечатан как принятый. Реестр: листы 6–11, вопросы К-26, К-25.
7. Номера помещений — по экспликации (лист 21); наименования и площади на этом листе не дублируются.
8. Марки текстиля «Т» и декора «Д» относятся только к листам текстиля и декора; индексы трубопроводов Т1–Т4 — на листах ВК и ОВ.

1000 мм · печать 1:1

| Изм. | Кол.уч | Лист | № док. | Подп. | Дата |
|---|---|---|---|---|---|
| Разраб. | | Кырпан А.С. | | | 05.10.26 |
| Пров. | | | | | |
| ГИП | | | | | |
| Н. контр. | | | | | |
| Утв. | | | | | |

**ГД-2026-003-АИ**

Трёхкомнатная квартира

Общая площадь 78,95* м² · * размеры со скана, не замерены (реестр — п. 6–11, К-13)

Дизайн-проект интерьера трёхкомнатной квартиры

| Стадия | Лист | Листов |
|---|---|---|
| РП | 55 | 94 |

План текстиля и декора

М 1:50

Кырпан Александр Сергеевич

выпуск 05.10.2026 · 6add39ab8d · стр. 64 из 137

08

# Декор и текстиль

Кырлан Александр Сергеевич

выпуск 05.10.2026 № 6add39ab8d · стр. 65 из 137

# Шторы и карнизы

Схемы окон «шина → полотно» (М 1:50) · отметки от чистого пола помещения · размеры в мм

**Окно 1 — Спальня 1 (пом. 1): Т1, Т2 (М 1:50)**

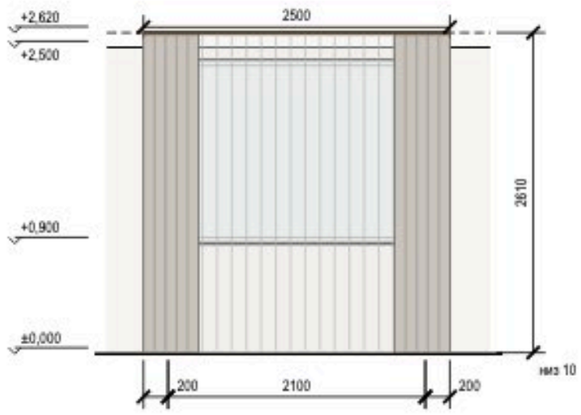


**Окно 1 — Спальня 2 (пом. 4): Т7, Т8 (М 1:50)**

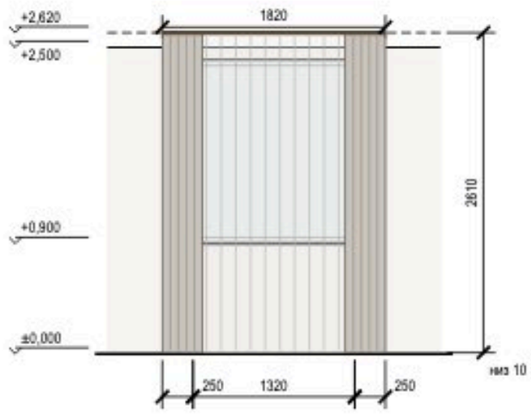


**Окно 1 — Кухня-гостиная (пом. 6): Т13, Т14 (М 1:50)**

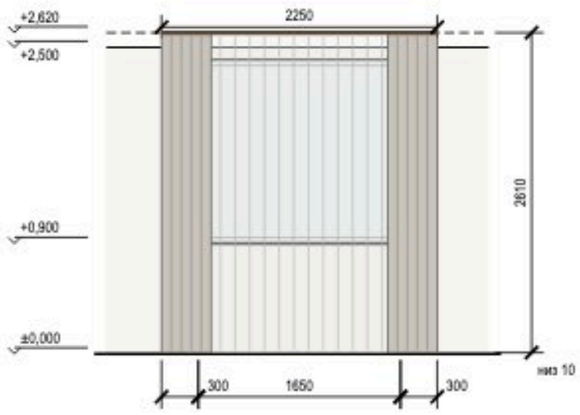


**Окно 2 — Кухня-гостиная (пом. 6): Т15 (М 1:50)**

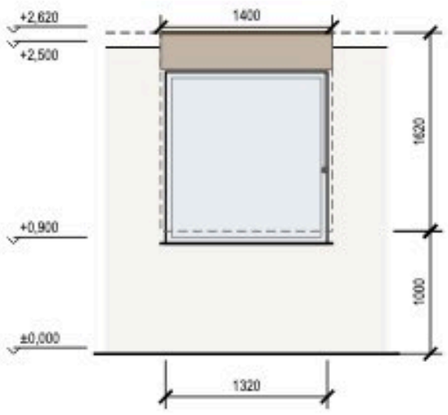


## Карта окон: окно → шина → полотно

| Поз. | Окно, пом. | Проём Ш×В, подоконник | Верх ниши | Изделие | Шина / карниз: длина, крепление | Верх шины | Полотно: длина, низ | Управление |
|---|---|---|---|---|---|---|---|---|
| Т1 | 1, пом. 1 | 2100×1500, подок. 900 | +2,620 | портьеры | шина, 2500, в нише потолка, вынос 150 | +2,620 | 2610, низ 10 (парит) | вручную |
| Т2 | 1, пом. 1 | 2100×1500, подок. 900 | +2,620 | тюль | шина, 2500, в нише потолка, вынос 150 | +2,620 | 2610, низ 10 (парит) | вручную |
| Т7 | 1, пом. 4 | 1320×1500, подок. 900 | +2,620 | портьеры | шина, 1820, в нише потолка, вынос 150 | +2,620 | 2610, низ 10 (парит) | вручную |
| Т8 | 1, пом. 4 | 1320×1500, подок. 900 | +2,620 | тюль | шина, 1820, в нише потолка, вынос 150 | +2,620 | 2610, низ 10 (парит) | вручную |
| Т13 | 1, пом. 6 | 1650×1500, подок. 900 | +2,620 | портьеры | шина, 2250, в нише потолка, вынос 150 | +2,620 | 2610, низ 10 (парит) | вручную |
| Т14 | 1, пом. 6 | 1650×1500, подок. 900 | +2,620 | тюль | шина, 2250, в нише потолка, вынос 150 | +2,620 | 2610, низ 10 (парит) | вручную |
| Т15 | 2, пом. 6 | 1320×1400, подок. 900 | +2,620 | римская штора | карниз, 1400, в нише потолка, вынос 60 | +2,620 | 1620, низ 1000 | шнур, петля низом 1500, натяжитель |

## Задания смежникам

| Кому | Задание | Пом. |
|---|---|---|
| Гипсокартонщик | окно 1 (2100×1500, Т1, Т2): ниша под шторы 150×120, верх +2,620; закладная под шину L 2500 по всей длине — до обшивки | 1 |
| Гипсокартонщик | окно 1 (1320×1500, Т7, Т8): ниша под шторы 150×120, верх +2,620; закладная под шину L 1820 по всей длине — до обшивки | 4 |
| Гипсокартонщик | окно 1 (1650×1500, Т13, Т14): ниша под шторы 150×120, верх +2,620; закладная под шину L 2250 по всей длине — до обшивки | 6 |
| Гипсокартонщик | окно 2 (1320×1400, Т15): ниша под шторы 150×120, верх +2,620; закладная под шину L 1400 по всей длине — до обшивки | 6 |
| Электрик | выводы под электрокарнизы не требуются (управление вручную) | |

## Условные обозначения

- портьеры в открытом положении
- римская штора: сложена / опущена
- верх ниш под шторы в потолке
- тюль (на виде окна — прозрачная плашка)
- шина или карниз на отметке верха
- оконный проём

**Допущения и предложения на листе**

Основа листа: размеры сняты со скана плана заказчика по размерным цепочкам, контрольный обмер на объекте не выполнялся (К-13); высота потолка 2700 мм принята: на плане заказчика не указана (К-11); толщины стен приняты: наружные 250 мм, перегородки 150 мм (на плане 85–190 мм) (К-13); разрешённая мощность 15 кВт принята по типовой квартире, технических условий нет (К-14); утолщение стены 190 × 1360 мм и элемент 1470 × 160 мм плана заказчика не определены (К-12); ниши санузла 2 закрыты перегородкой и фальш-стеной: проектное решение, на плане заказчика ниша у входа открыта (К-18); несущие стены не определены: до технического заключения все существующие стены считаются несущими (К-20); окна существующие и сохраняются; подоконная доска и глубина откосов не заданы — приняты, не замерены (К-27).

См. лист открытых вопросов (лист 6, запись К-11; лист 7, записи К-12–К-14, К-18, К-20; лист 8, запись К-27).

## Примечания

1. Отметки — от чистого пола помещения; размеры — мм. Длины полотен уточняются замером после чистовой отделки пола и потолка, до раскроя.
2. Шины в нишах потолка: закладная (брус или профиль) по всей длине ниши — до обшивки ГКЛ; ниша и её отметка — узел ниши на плане потолков (лист 44).
3. Шина в нише — на отметке верха ниши (крепление к закладной в потолке ниши); длина полотна — от верха шины до чистого пола за вычетом зазора.
4. Полотно портьер «парит» над полом на 10 мм; сборка портьер — 2,0, тюля — 2,5 (ширина полотна — в ведомости текстиля).
5. Шнур римской шторы — с натяжителем, петля низом не ниже 1500 мм от пола (защита детей; EN 13120 — рекомендация).
6. Электрокарнизы не предусмотрены; при замене на электропривод — вывод кабеля в нише у края шины (задание электрику).
7. Марки изделий — по плану текстиля и декора (лист 55) и ведомости текстиля (лист 57).

| Изм. | Кол.уч | Лист | № док. | Подп. | Дата |
|---|---|---|---|---|---|
| Разраб. | | Кырпан А.С. | | | 05.10.26 |
| Пров. | | | | | |
| ГИП | | | | | |
| | | | | | |
| Н. контр. | | | | | |
| Утв. | | | | | |

**ГД-2026-003-АИ**

Трёхкомнатная квартира

Общая площадь 78,95* м² · * размеры со скана, не замерены (реестр — п. 6–11, К-13)

Дизайн-проект интерьера трёхкомнатной квартиры

| Стадия | Лист | Листов |
|---|---|---|
| РП | 56 | 94 |

**Шторы и карнизы**

М 6/м

Кырпан Александр Сергеевич

выпуск 05.10.2026 · 6add39ab8d · стр. 66 из 137

# Ведомость текстиля

Шторы, тюль, римские шторы, ковры, подушки и пледы · размеры в мм · марки — по плану текстиля и декора

## Текстиль: шторы, ковры, подушки, пледы

| Поз. | Пом. | Изделие | Размер, мм | Ткань, состав, плотность | Сборка, ширина полотна | | Цвет (система, код) | Кол. | Примечание |
|---|---|---|---|---|---|---|---|---|---|
| T1 | 1 | Портьеры-волна | шина 2500 × полотно 2610 | лён с блэкаут-подкладкой; лён 100 %; 320 г/м² | × 2, ширина 5000 | | Tikkurila H487 (Pumice) | 2 | низ 10 (парит); в нише потолка |
| T2 | 1 | Тюль | шина 2500 × полотно 2610 | вуаль; полиэстер 100 % | × 2,5, ширина 6250 | | Tikkurila V503 (Winter) | 1 | низ 10 (парит); в нише потолка |
| T3 | 1 | Ковёр под кроватью | 2800×1850 | шерсть, ручное ткачество; шерсть 80 %, хлопок 20 % | | | NCS S 3005-Y20R (тёплый таупе-серый) | 1 | противоскользящая подложка; ворс 10 мм |
| T4 | 1 | Подушки декоративные на кровать | 500×500 | лён 100 % | | | Tikkurila H487 (Pumice) | 3 | на C1 |
| T5 | 1 | Подушки на кровать, акцент | 400×600 | хлопковый бархат 100 % | | | Farrow & Ball No. 30 (Hague Blue) | 2 | на C1 |
| T6 | 1 | Плед на кровать | 1300×1700 | шерсть мериноса 100 % | | | Farrow & Ball No. 30 (Hague Blue) | 1 | на C1 |
| T7 | 4 | Портьеры-волна | шина 1820 × полотно 2610 | лён с блэкаут-подкладкой; лён 100 %; 320 г/м² | × 2, ширина 3640 | | Tikkurila H487 (Pumice) | 2 | низ 10 (парит); в нише потолка |
| T8 | 4 | Тюль | шина 1820 × полотно 2610 | вуаль; полиэстер 100 % | × 2,5, ширина 4550 | | Tikkurila V503 (Winter) | 1 | низ 10 (парит); в нише потолка |
| T9 | 4 | Ковёр под кроватью | 2500×1800 | шерсть, плоское плетение; шерсть 100 % | | | Tikkurila V484 (Driftwood) | 1 | противоскользящая подложка; ворс 8 мм |
| T10 | 4 | Подушки декоративные на кровать | 500×500 | буклé (шерсть 60 %, полиэстер 40 %) | | | Farrow & Ball No. 229 (Elephant's Breath) | 3 | на C7 |
| T11 | 4 | Подушки на кровать, акцент | 400×600 | хлопковый бархат 100 % | | | Farrow & Ball No. 47 (Green Smoke) | 2 | на C7 |
| T12 | 4 | Плед на кровать | 1300×1700 | шерсть мериноса 100 % | | | Farrow & Ball No. 30 (Hague Blue) | 1 | на C7 |
| T13 | 6 | Портьеры-волна (гостиная) | шина 2250 × полотно 2610 | лён 70 %, вискоза 30 %; 280 г/м² | × 2, ширина 4500 | | Tikkurila H487 (Pumice) | 2 | низ 10 (парит); в нише потолка |
| T14 | 6 | Тюль (гостиная) | шина 2250 × полотно 2610 | вуаль; полиэстер 100 % | × 2,5, ширина 5625 | | Tikkurila V503 (Winter) | 1 | низ 10 (парит); в нише потолка |
| T15 | 6 | Римская штора (кухня) | карниз 1400 × полотно 1620 | лён 100 % | | | Tikkurila V484 (Driftwood) | 1 | низ 1000; в нише потолка; шнур: петля 1500, натяжитель |
| T16 | 6 | Ковёр в зоне отдыха | 3000×1150 | шерсть, петля; шерсть 100 % | | | Tikkurila V484 (Driftwood) | 1 | противоскользящая подложка; ворс низкий |
| T17 | 6 | Подушки на диван | 500×500 | буклé (шерсть 60 %, полиэстер 40 %) | | | Tikkurila H487 (Pumice) | 3 | на M2 |
| T18 | 6 | Подушки на диван, акцент | 400×600 | хлопковый бархат 100 % | | | Farrow & Ball No. 30 (Hague Blue) | 2 | на M2 |
| T19 | 6 | Плед на диван | 1300×1700 | альпака 50 %, шерсть 50 % | | | Tikkurila V484 (Driftwood) | 1 | на M2 |

образец цвета — по HEX производителя краски, справочно

Итого: шторы и тюль — 10 шт.; ковры и дорожки — 3 шт.; подушки, пледы, покрывала — 18 шт.

## Образцы по помещениям

**1. Спальня 1**

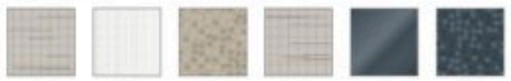

T1 T2 T3 T4 T5 T6

**4. Спальня 2**

T7 T8 T9 T10 T11 T12

**6. Кухня-гостиная**

T13 T14 T15 T16 T17 T18 T19

**Допущения и предложения на листе**

Основа листа: размеры сняты со скана плана заказчика по размерным цепочкам, контрольный обмер на объекте не выполнялся (К-13); высота потолка 2700 мм принята: на плане заказчика не указана (К-11); толщины стен приняты: наружные 250 мм, перегородки 150 мм (на плане 85–190 мм) (К-13); разрешённая мощность 15 кВт принята по типовой квартире, технических условий нет (К-14); утолщение стены 190 × 1360 мм и элемент 1470 × 160 мм плана заказчика не определены (К-12); ниши санузла 2 закрыты перегородкой и фальш-стеной: проектное решение, на плане заказчика ниша у входа открыта (К-18); несущие стены не определены: до технического заключения все существующие стены считаются несущими (К-20); окна существующие и сохраняются; подоконная доска и глубина откосов не заданы — приняты, не замерены (К-27).

См. лист открытых вопросов (лист 6, запись К-11; лист 7, записи К-12–К-14, К-18, К-20; лист 8, запись К-27).

## Примечания

1. Коды цвета — ориентир подбора по веерам производителей красок; ткань утверждается по образцу при дневном свете и при свете проекта 2700–3000 К.
2. Размеры полотен — по замеру после чистовой отделки пола и потолка; ширина полотна указана с учётом сборки, без припусков на швы. Схемы окон и отметки шин — лист 56.
3. Портьеры и тюль — на тесьме «волна» по системе шины; блэкаут — подкладкой. Ковры — на противоскользящей подложке.
4. Замена изделия — аналогом по характеристикам (состав, плотность, размер, цвет по образцу) с согласованием автора проекта.
5. Места изделий — план текстиля и декора (лист 55); подушки и пледы — по марке мебели.

| Изм. | Кол.уч | Лист | № док. | Подп. | Дата |
|---|---|---|---|---|---|
| Разраб. | | Кырпан А.С. | | | 05.10.26 |
| Пров. | | | | | |
| ГИП | | | | | |
| | | | | | |
| Н. контр. | | | | | |
| Утв. | | | | | |

**ГД-2026-003-АИ**

Трёхкомнатная квартира

Общая площадь 78,95* м² · * размеры со скана, не замерены (реестр — п. 6–11, К-13)

Дизайн-проект интерьера трёхкомнатной квартиры

| Стадия | Лист | Листов |
|---|---|---|
| РП | 57 | 94 |

**Ведомость текстиля**

М 6/м

Кырпан Александр Сергеевич

выпуск 05.10.2026 · 6add39ab8d · стр. 67 из 137

# Ведомость декора. Схемы развески

Картины, зеркала, растения, настольный декор · схемы развески (М 1:50) · высоты — мм от чистого пола

## Декор: картины, зеркала, растения, предметы

картина · зеркало · мебель под изделием

| Поз. | Пом. | Предмет | Размер, мм | Место: стена, высота от пола, мм | Масса, кг | Крепёж и основание | Свет места, отделка | Кол. |
|---|---|---|---|---|---|---|---|---|
| ДК1 | 1 | Картина над кроватью | 1200×700 | стена А, привязка 2250; низ 1300, центр 1650; над С1 | 4 | подвес по основанию, 2 точки | рама — дуб | 1 |
| ДК2 | 2 | Зеркало над умывальником, алагостойкое | 600×750 | стена Г, привязка 1150; низ 1100, центр 1475 | 4 | подвес по основанию, 2 точки | | 1 |
| ДК3 | 4 | Картина над кроватью | 1000×700 | стена А, привязка 1545; низ 1300, центр 1650; над С7 | 4 | подвес по основанию, 2 точки | рама — дуб | 1 |
| ДК4 | 4 | Зеркало в рост в тонкой чёрной раме | 600×1600 | стена Г, привязка 700; низ 300, центр 1100 | 12 | анкер для пустотелых оснований, 4 шт.; основание: перегородка — определить обмером до монтажа; нагрузка 30 кг | рама — чёрный матовый металл | 1 |
| ДК5 | 5 | Зеркало | 800×1800 | стена Б, привязка 525; низ 550, центр 1450 | 18 | анкер, 4 шт.; основание: перегородка — определить обмером до монтажа; нагрузка 40 кг | рама — чёрный матовый металл | 1 |
| ДК6 | 6 | Картина | 1200×900 | стена Г, привязка 725; центр 1550 | 6 | анкер, 2 шт.; основание: перегородка — определить обмером до монтажа; нагрузка 15 кг | | 1 |
| ДК7 | 6 | Растение | 450×450 | напольное | | | свет средний | 1 |
| ДК8 | 6 | Ваза керамическая с ветками на обеденном столе | 200×350 | на М5 (обеденный стол) | | | | 1 |
| ДК9 | 7 | Зеркало над умывальником, алагостойкое | 500×700 | стена Б, привязка 780; низ 1100, центр 1450 | 4 | подвес по основанию, 2 точки | | 1 |

**ДК1 — Спальня 1 (пом. 1), стена А (М 1:50)**

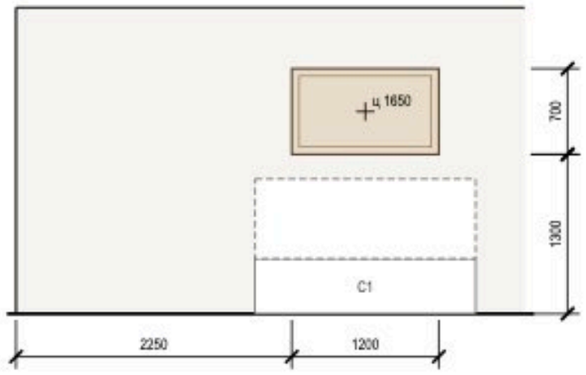


**ДК2 — Ванная (пом. 2), стена Г (М 1:50)**

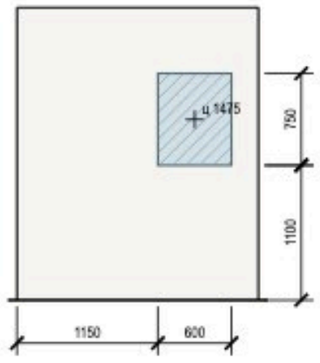


**ДК3 — Спальня 2 (пом. 4), стена А (М 1:50)**

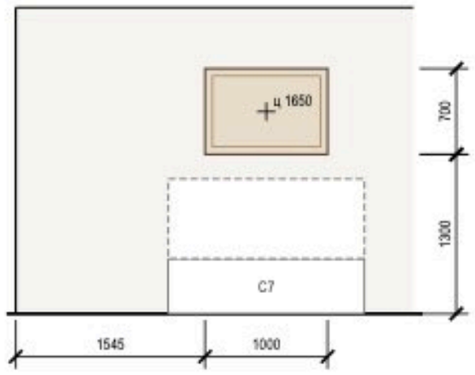


**ДК4 — Спальня 2 (пом. 4), стена Г (М 1:50)**

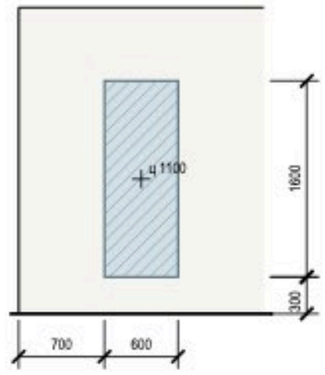


**ДК5 — Прихожая (пом. 5), стена Б (М 1:50)**

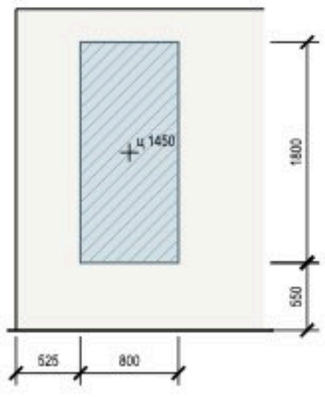


**ДК6 — Кухня-гостиная (пом. 6), стена Г (М 1:50)**

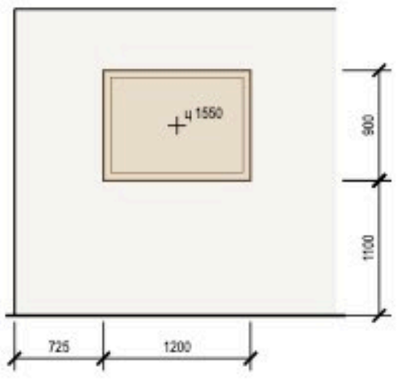


**ДК9 — Санузел 2 (пом. 7), стена Б (М 1:50)**

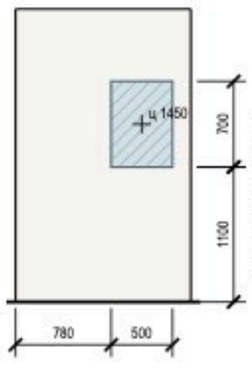


**Допущения и предложения на листе**

Основа листа: размеры сняты со скана плана заказчика по размерным цепочкам, контрольный обмер на объекте не выполнялся (К-13); высота потолка 2700 мм принята: на плане заказчика не указана (К-11); толщины стен приняты: наружные 250 мм, перегородки 150 мм (на плане 85–190 мм) (К-13); разрешённая мощность 15 кВт принята по типовой квартире, технических условий нет (К-14); утолщение стены 190 × 1360 мм и элемент 1470 × 160 мм плана заказчика не определены (К-12); ниши санузла 2 закрыты перегородкой и фальш-стеной: проектное решение, на плане заказчика ниша у входа открыта (К-18); несущие стены не определены: до технического заключения все существующие стены считаются несущими (К-20); окна существующие и сохраняются; подоконная доска и глубина откосов не заданы — приняты, не замерены (К-27).
См. лист открытых вопросов (лист 6, запись К-11; лист 7, записи К-12–К-14, К-18, К-20; лист 8, запись К-27).

## Примечания

1. Высоты — от чистого пола помещения до низа изделия, «ц» — до центра; привязки — от чистовой грани угла стены, мм.
2. Над мебелью низ изделия — на 150–250 мм выше спинки или изголовья; без мебели центр — на 1450–1600 мм от пола.
3. Изделия до 5 кг — на два подвеса по основанию; тяжелее — на анкеры с нагрузкой не меньше двойной массы; на ГКЛ — только по закладной или анкеру для пустотелых оснований.
4. Зеркала в рост — с креплением от опрокидывания; в санузлах — влагостойкие, на клей для зеркал и нейтральный силикон.
5. Места изделий — план текстиля и декора (лист 55).

| Изм. | Кол.уч | Лист | № док. | Подп. | Дата |
|---|---|---|---|---|---|
| Разраб. | | Кырпан А.С. | | | 05.10.26 |
| Пров. | | | | | |
| ГИП | | | | | |
| | | | | | |
| Н. контр. | | | | | |
| Утв. | | | | | |

**ГД-2026-003-АИ**

Трёхкомнатная квартира

Общая площадь 78,95* м² · * размеры со скана, не замерены (реестр — п. 6–11, К-13)

Дизайн-проект интерьера трёхкомнатной квартиры

| Стадия | Лист | Листов |
|---|---|---|
| РП | 58 | 94 |

Ведомость декора. Схемы развески

М 6/м

Кырпан Александр Сергеевич

выпуск 05.10.2026 № 6add39ab8d · стр. 68 из 137

# Встроенная мебель. Схема расположения

встроенная и корпусная мебель на заказ, кухонный гарнитур · размеры в мм · марки — по ведомости изделий

ПРЕДВАРИТЕЛЬНО · не для производства работ · открыто пунктов: 31 (реестр — л. 6–11)

## Ведомость изделий

| Марка | Наименование | Пом. | Ш×Г×В, мм | Лист |
|---|---|---|---|---|
| С5 | Шкаф распашной | 1 | 1900×600×2400 | 60 |
| Г1 | Система хранения | 3 | 1700×600×2400 | 61 |
| М16 | Шкаф-купе | 5 | 1800×600×2600 | 62 |
| М6* | Модуль нижний: карго, духовой шкаф, ящики, варочная | 6 | 1800×600×900 | 63 |
| М15** | Модуль навесной: полки | 6 | 600×400×600 | 63 |
| М13 | Модуль навесной: полки, сушка | 6 | 2200×350×720 | 63 |
| М14* | Модуль нижний: ПММ | 6 | 600×600×900 | 63 |
| М7* | Модуль нижний: мойка | 6 | 800×600×900 | 63 |
| М8* | Пенал: холодильник встр. | 6 | 600×650×2100 | 63 |

## Условные обозначения

- изделие мебельщика: корпус на полу
- навесной модуль (невидимый контур)
- открывание распашного фасада
- зона выдвижения ящика, двери техники
- дверь купе, стрелка — направление движения
- (П5) марка изделия, под ней — лист изделия
- ★ «*» — принято, не замерено и не подтверждено

Допущения и предложения на листе. Основа листа: размеры сняты со скана плана заказчика по размерным цепочкам, контрольный обмер на объекте не выполнялся (К-13); высота потолка 2700 мм принята: на плане заказчика не указана (К-11); толщины стен приняты: наружные 250 мм, перегородки 150 мм (на плане 85–190 мм) (К-13); разрешённая мощность 15 кВт принята по типовой квартире, технических условий нет (К-14); утолщение стены 190 × 1360 мм и элемент 1470 × 160 мм плана заказчика не определены (К-12); ниши санузла 2 закрыты перегородкой и фальш-стеной: проектное решение, на плане заказчика ниша у входа открыта (К-18); несущие стены не определены: до технического заключения все существующие стены считаются несущими (К-20); окна существующие и сохраняются; подоконная доска и глубина откосов не заданы — приняты, не замерены (К-27). Знак «*» — принято, не замерено и не подтверждено (замерить на объекте): К-17: Ст К1-1, Ст В1-1, Ст К1-2, Ст В1-2. Знак «**» — предложение проектировщика, заказчиком не утверждено (согласовать с заказчиком). См. лист открытых вопросов (лист 6, записи К-8, К-11; лист 7, записи К-12–К-14, К-17, К-18, К-20; лист 8, записи К-25–К-27; лист 9, запись ИЗ-5).

## Примечания

1. Изделия — по чистовым размерам помещений; перед раскроем — контрольный замер цеха после чистовой отделки стен, пола и потолка.
2. Открывание фасадов и выдвижение ящиков показано в открытом положении: зоны не пересекают двери, радиаторы, выключатели и проходы.
3. Столяки и счётчики за мебелью — с сервисным люком; газовые трубы мебелью не зашиваются.
4. Покупная мебель — по плану расстановки мебели и спецификации дизайнера; здесь — подложкой.
5. Допущение проекта: кухня: раскладка гарнитура принята проектной, решение автора (ИЗ-12) — мойка М7* у шахты Ш2, ПММ М14* рядом с мойкой, варочная и духовой шкаф в М8*, вытяжка М15**, холодильник М6**; выводы техники — по типовой расстановке; условие: до начала черновых работ сверить раскладку и выводы с чертежом кухни от изготовителя, выводы пересматриваются по его чертежу (вопрос К-8).
6. Марки из допущений, которых нет на этом листе: Ш2 — лист 39.
7. Знак «*» у проёма — допущение: положение проёма не замерено (дверь пом. 5, стена В; дверь пом. 8, стена А (2 шт.)); размер напечатан как принятый. Реестр: листы 6–11, вопросы К-26, К-25.

1000 мм · печать 1:1

| Изм. | Кол.уч | Лист | № док. | Подп. | Дата |
|---|---|---|---|---|---|
| Разраб. | | Кырпан А.С. | | | 05.10.26 |
| Пров. | | | | | |
| ГИП | | | | | |
| | | | | | |
| Н. контр. | | | | | |
| Утв. | | | | | |

**ГД-2026-003-АИ**

Трёхкомнатная квартира

Общая площадь 78,95* м² · * размеры со скана, не замерены (реестр — п. 6–11, К-13)

| Дизайн-проект интерьера трёхкомнатной квартиры | Стадия | Лист | Листов |
|---|---|---|---|
| | РП | 59 | 94 |
| **Встроенная мебель. Схема расположения** М 1:50 | **Кырпан Александр Сергеевич** | | |

выпуск 05.10.2026 № 6add39ab8d · стр. 69 из 137

# Шкаф распашной С5

Спальня 1 (пом. 1) · вид из помещения · размеры в мм, отметки в м

ПРЕДВАРИТЕЛЬНО · не для производства работ · открыто пунктов: 31 (реестр — л. 6–11)

**Вид с фасадами**

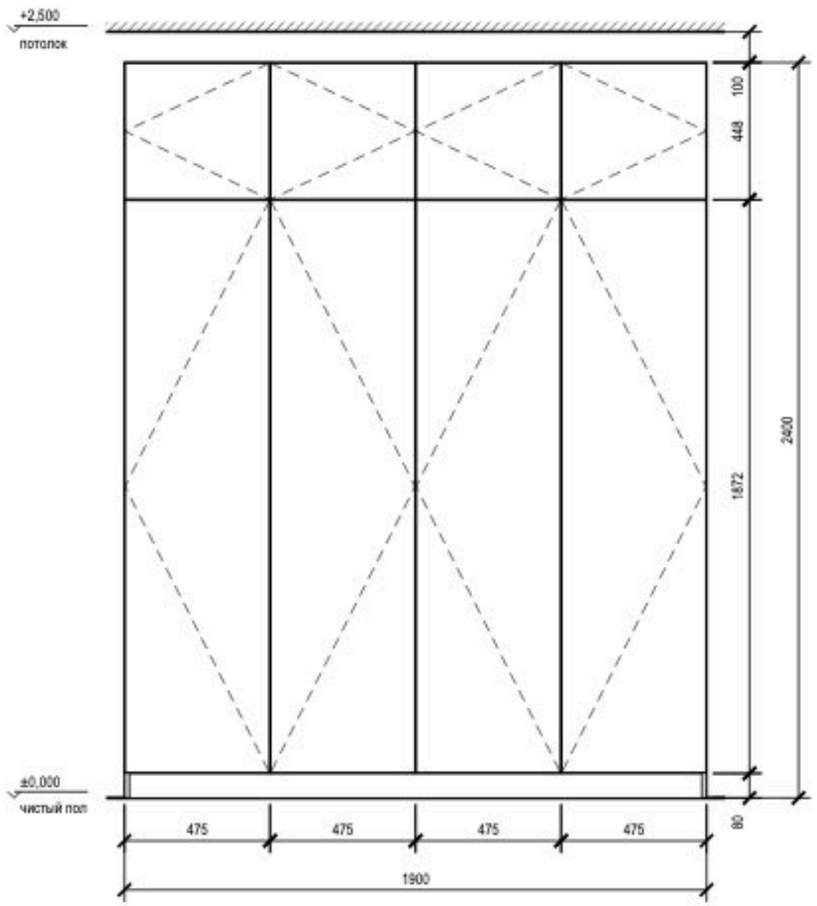


**Вид без фасадов**

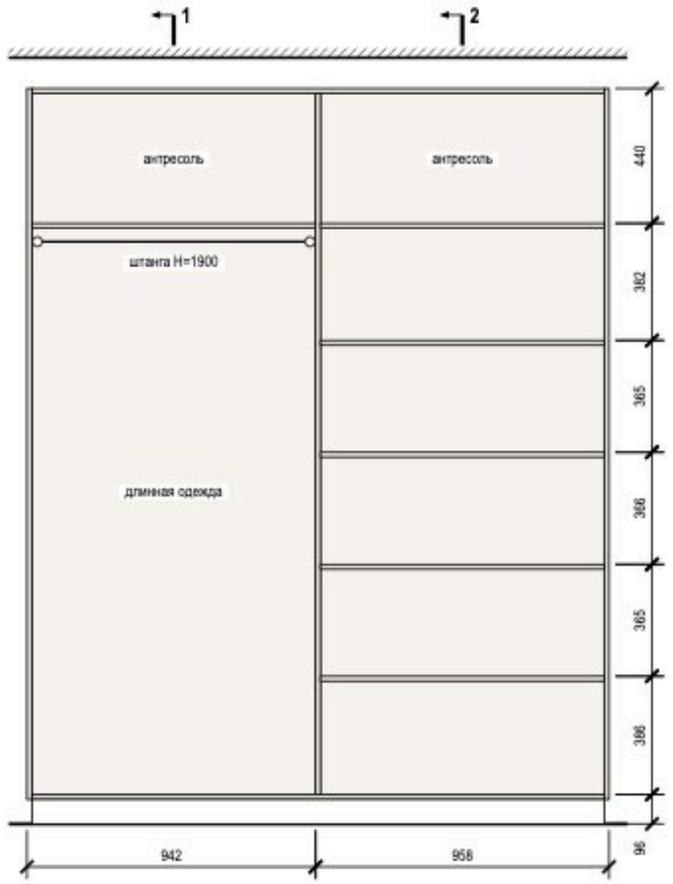


**Разрез 1-1**

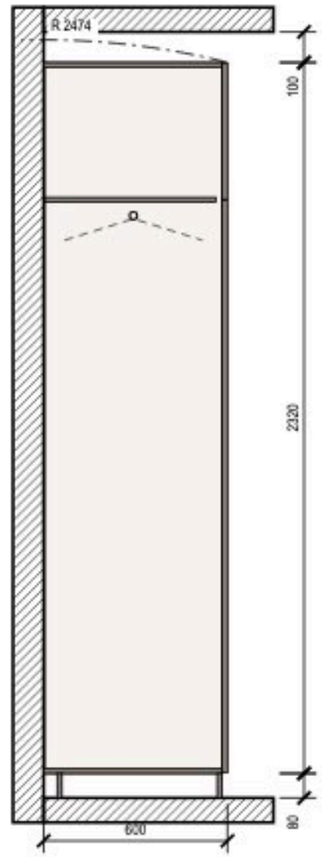


**Разрез 2-2**

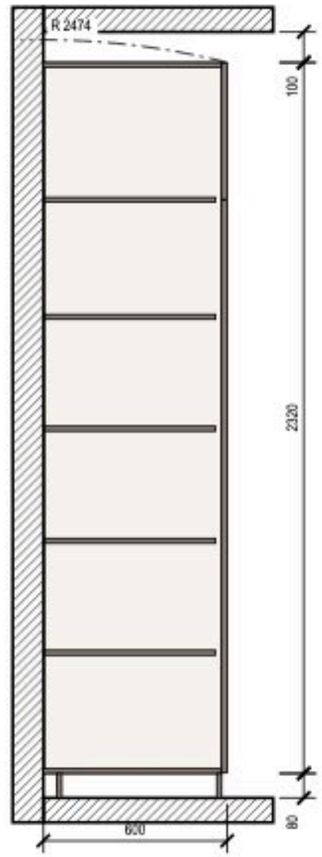


## Примечания

1. Размеры — в мм по чистовой отделке; изделие 1900×600×2400 (Ш×Г×В). Перед раскроем — контрольный замер цеха после чистовой отделки стен, пола и потолка.
2. Корпус — ЛДСП 16 мм, задняя стенка ХДФ 4 мм в паз, цоколь 80 мм на регулируемых опорах; фасады — МДФ, эмаль матовая 18 мм накладные, цвет — по колерной карте; петли с доводчиком: фасад 1869 мм — 4 петли, фасад 445 мм — 2 петли.
3. Кромка: скрытые торцы 0,4 мм, видимые 2 мм (ПВХ/АБС).
4. Номинальные зазоры: между фасадами 3 мм, фасад — стена и фасад — потолок не менее 3 мм, фасад ящика — стойка 2 мм.
5. Ящики — направляющие полного выдвижения NL 550 (внутренняя глубина 578 мм ≥ NL + 3); присадка по 32-й системе — выполняет цех.
6. Зазор до потолка 100 мм — закрыть планкой в цвет корпуса при монтаже.
7. Подъём корпуса: диагональ боковины $\sqrt{2400^2 + 600^2}$ = 2474 мм < 2500 мм до потолка — корпус собирается лёжа и поднимается поворотом.
8. Крепление к стене от опрокидывания: уголок к стене, 2 шт.; основание стены и шаг анкеров — монтажная схема шкафов.

## Условные обозначения

- фасад распашной: линии сходятся к стороне петель
- корпус и полки ЛДСП (вид на стену)
- задняя стенка ХДФ
- деталь в разрезе
- штанга для плечиков (на разрезе — плечики 450 мм)
- траектория угла корпуса при подъёме в проектное положение

**Допущения и предложения на листе**

Основа листа: размеры сняты со скана плана заказчика по размерным цепочкам, контрольный обмер на объекте не выполнялся (К-13); высота потолка 2700 мм принята: на плане заказчика не указана (К-11); толщины стен приняты: наружные 250 мм, перегородки 150 мм (на плане 85–190 мм) (К-13); разрешённая мощность 15 кВт принята по типовой квартире, технических условий нет (К-14); утолщение стены 190 × 1360 мм и элемент 1470 × 160 мм плана заказчика не определены (К-12); ниши санузла 2 закрыты перегородкой и фальш-стеной: проектное решение, на плане заказчика ниша у входа открыта (К-18); несущие стены не определены: до технического заключения все существующие стены считаются несущими (К-20); окна существующие и сохраняются; подоконная доска и глубина откосов не заданы — приняты, не замерены (К-27).
См. лист открытых вопросов (лист 6, запись К-11; лист 7, записи К-12–К-14, К-18, К-20; лист 8, запись К-27).

1000 мм · печать 1:1

| Изм. | Кол.уч | Лист | № док. | Подп. | Дата |
|---|---|---|---|---|---|
| Разраб. | | Кырпан А.С. | | | 05.10.26 |
| Пров. | | | | | |
| ГИП | | | | | |
| | | | | | |
| Н. контр. | | | | | |
| Утв. | | | | | |

**ГД-2026-003-АИ**

Трёхкомнатная квартира

Общая площадь 78,95* м² · * размеры со скана, не замерены (реестр — п. 6–11, К-13)

Дизайн-проект интерьера трёхкомнатной квартиры

| Стадия | Лист | Листов |
|---|---|---|
| РП | 60 | 94 |

**Шкаф распашной С5**

М 1:20

Кырпан Александр Сергеевич

выпуск 05.10.2026 № 6add39a08d · стр. 70 из 137

# Система хранения Г1

Гардеробная (пом. 3) · вид из помещения · размеры в мм, отметки в м

ПРЕДВАРИТЕЛЬНО · не для производства работ · открыто пунктов: 31 (реестр — л. 6–11)

**Общий вид**

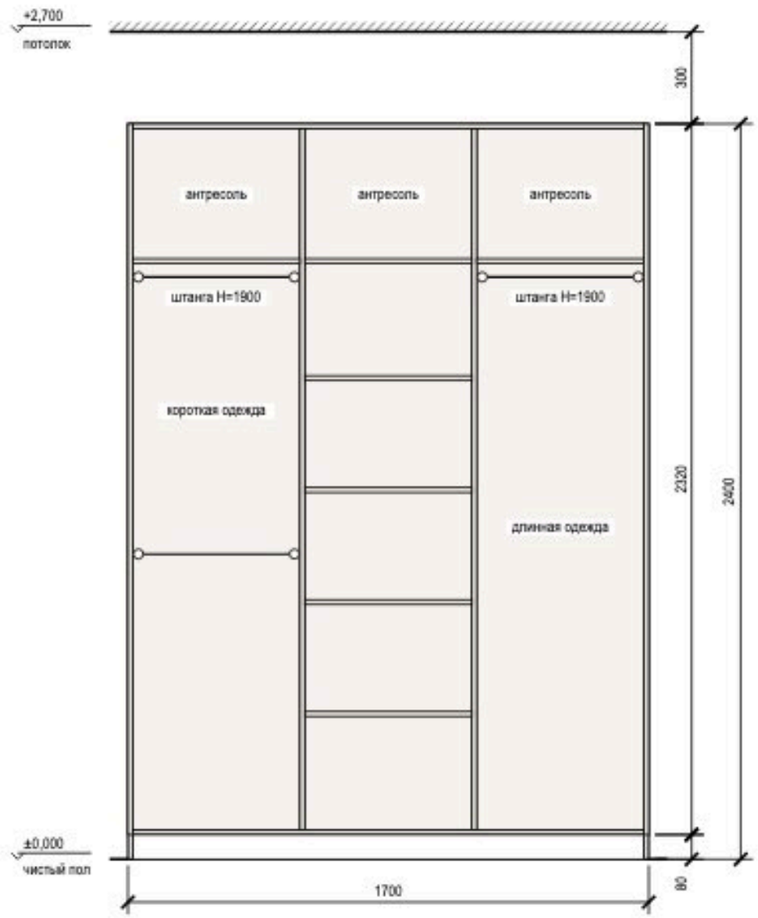


**Наполнение, размеры в свету**

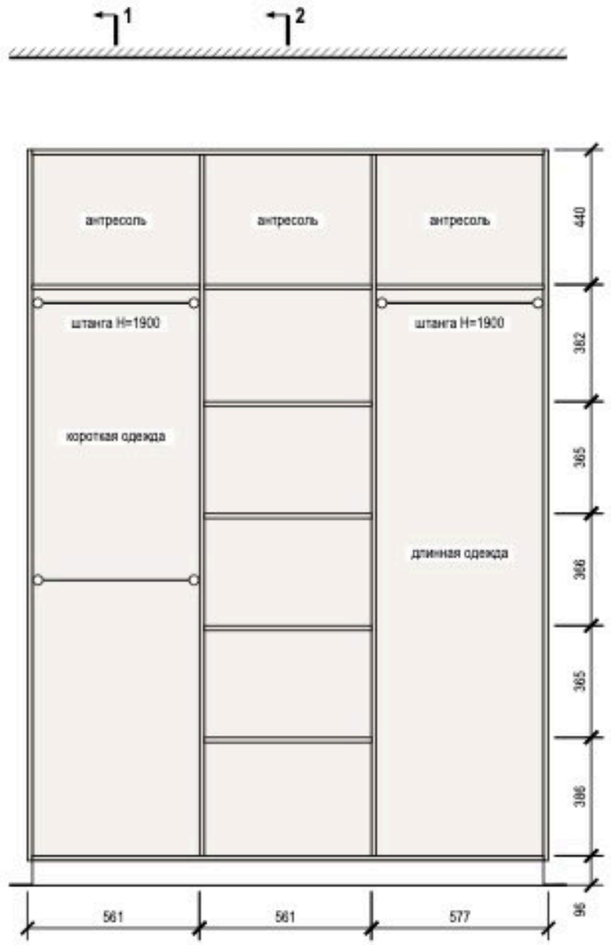


**Разрез 1-1**

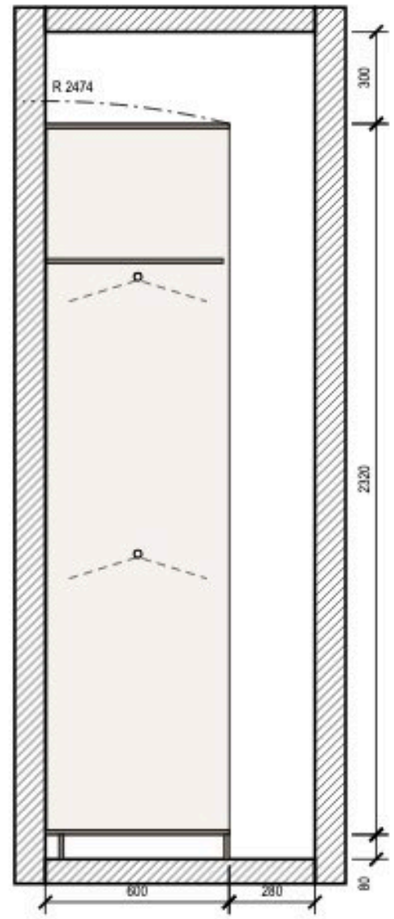


**Разрез 2-2**

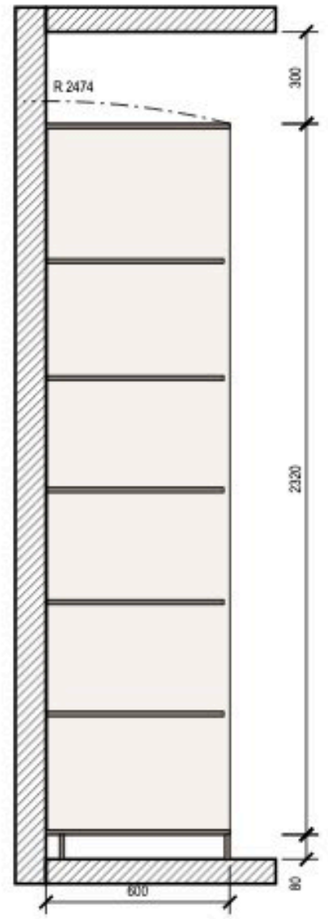


## Примечания

1. Размеры — в мм по чистовой отделке; изделие 1700×600×2400 (Ш×Г×В). Перед раскроем — контрольный замер цеха после чистовой отделки стен, пола и потолка.
2. Корпус — ЛДСП 16 мм, задняя стенка ХДФ 4 мм в паз, цоколь 80 мм на регулируемых опорах; открытая система без фасадов, ящики с фасадами.
3. Кромка: скрытые торцы 0,4 мм, видимые 2 мм (ПВХ/АБС).
4. Номинальные зазоры: между фасадами ящиков 3 мм, фасад ящика — стойка 2 мм.
5. Ящики — направляющие полного выдвижения NL 550 (внутренняя глубина 596 мм ≥ NL + 3); присадка по 32-й системе — выполняет цех.
6. Зазор до потолка 300 мм.
7. Подъём корпуса: диагональ боковины √(2400² + 600²) = 2474 мм < 2700 мм до потолка — корпус собирается лёжа и поднимается поворотом.
8. Крепление к стене от опрокидывания: крепление к стене, 3 точки; основание стены и шаг анкеров — монтажная схема шкафов.
9. Проход перед изделием 280 мм показан на разрезе 1-1: меньше 600 мм — глубину уменьшить (торцевые штанги при глубине 350–450 мм) или изменить расстановку.

## Условные обозначения

- корпус и полки ЛДСП (вид на стену)
- задняя стенка ХДФ
- деталь в разрезе
- штанга для плечиков (на разрезе — плечики 450 мм)
- траектория угла корпуса при подъёме в проектное положение

**Допущения и предложения на листе**

Основа листа: размеры сняты со скана плана заказчика по размерным цепочкам, контрольный обмер на объекте не выполнялся (К-13); высота потолка 2700 мм принята: на плане заказчика не указана (К-11); толщины стен приняты: наружные 250 мм, перегородки 150 мм (на плане 85–190 мм) (К-13); разрешённая мощность 15 кВт принята по типовой квартире, технических условий нет (К-14); утолщение стены 190 × 1360 мм и элемент 1470 × 160 мм плана заказчика не определены (К-12); ниши санузла 2 закрыты перегородкой и фальш-стеной: проектное решение, на плане заказчика ниша у входа открыта (К-18); несущие стены не определены: до технического заключения все существующие стены считаются несущими (К-20); окна существующие и сохраняются; подоконная доска и глубина откосов не заданы — приняты, не замерены (К-27).

Открытые вопросы и конфликты по листу: К-9.

См. лист открытых вопросов (лист 6, записи К-9, К-11; лист 7, записи К-12–К-14, К-18, К-20; лист 8, запись К-27).

1000 мм · печать 1:1

| Изм. | Кол.уч | Лист | № док. | Подп. | Дата |
|---|---|---|---|---|---|
| Разраб. | | Кырпан А.С. | | | 05.10.26 |
| Пров. | | | | | |
| ГИП | | | | | |
| | | | | | |
| Н. контр. | | | | | |
| Утв. | | | | | |

**ГД-2026-003-АИ**

Трёхкомнатная квартира

Общая площадь 78,95* м² · * размеры со скана, не замерены (реестр — л. 6–11, К-13)

Дизайн-проект интерьера трёхкомнатной квартиры

| Стадия | Лист | Листов |
|---|---|---|
| РП | 61 | 94 |

**Система хранения Г1**

М 1:20

Кырпан Александр Сергеевич

выпуск 05.10.2026 № 6add39ab8d · стр. 71 из 137

# Шкаф-купе М16

Прихожая (пом. 5) · вид из помещения · размеры в мм, отметки в м

ПРЕДВАРИТЕЛЬНО · не для производства работ · открыто пунктов: 31 (реестр — л. 6–11)

**Вид с фасадами**

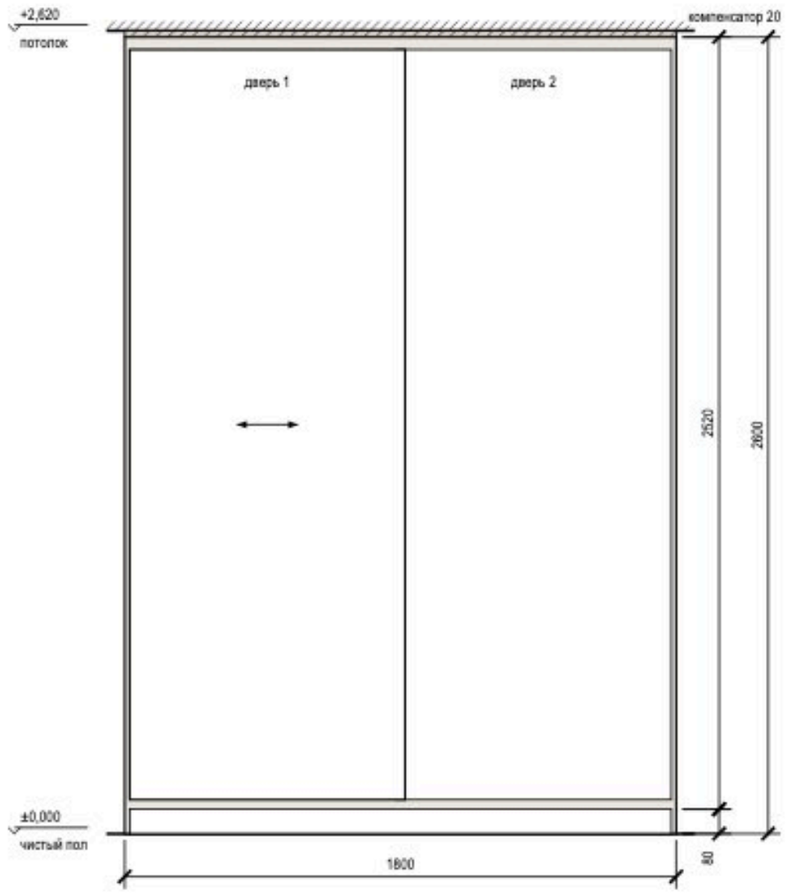


**Вид без фасадов**

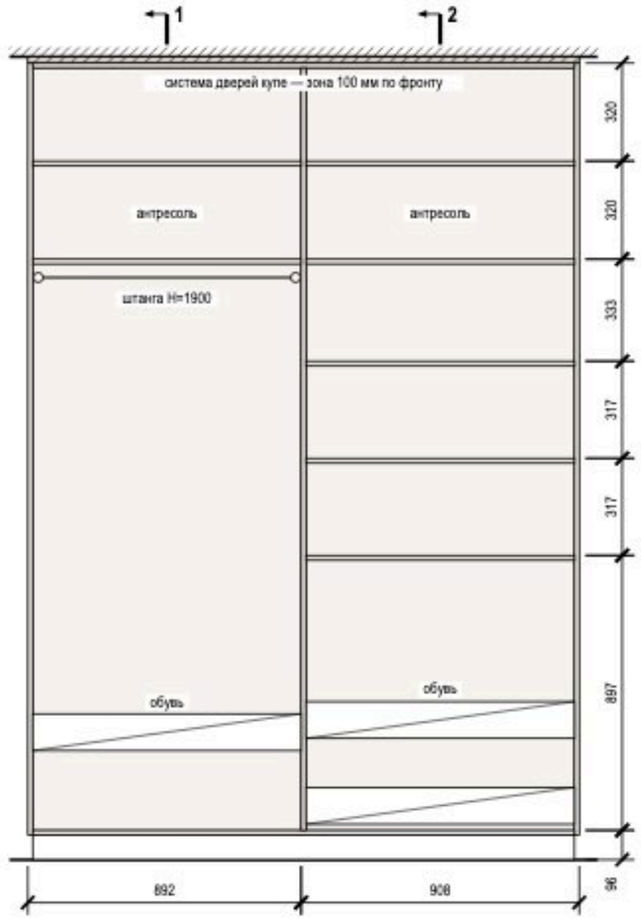


**Разрез 1-1**

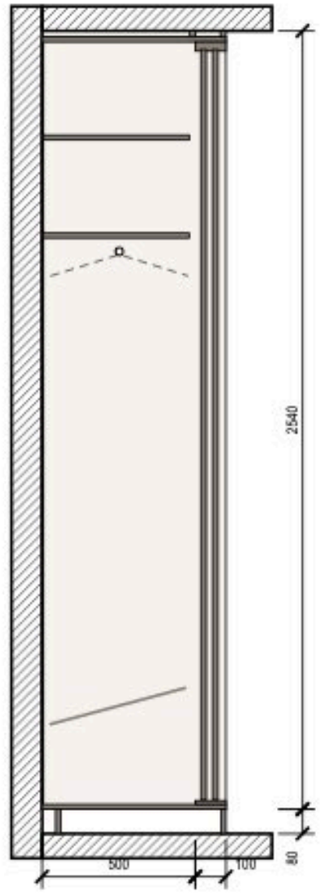


**Разрез 2-2**

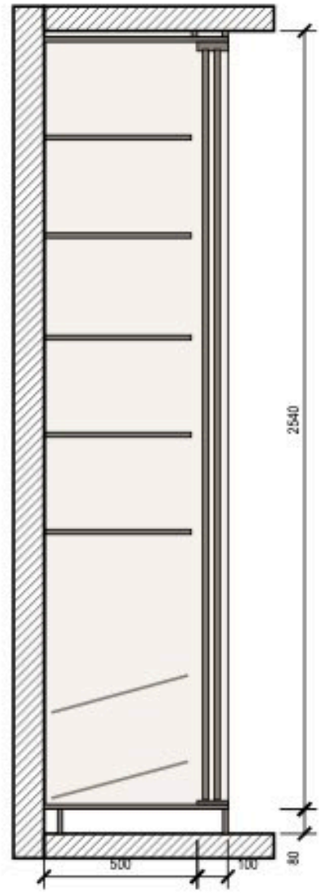


## Примечания

1. Размеры — в мм по чистовой отделке; изделие 1800×600×2600 (Ш×Г×В). Перед раскроем — контрольный замер цеха после чистовой отделки стен, пола и потолка.
2. Корпус — ЛДСП 16 мм, задняя стенка ХДФ 4 мм в паз, цоколь 80 мм на регулируемых опорах; двери купе — ЛДСП 10 мм в алюминиевом профиле, нахлёст 30 мм, ширина двери 899 мм, высота — проём минус 40 мм; цвет — по колерной карте.
3. Кромка: скрытые торцы 0,4 мм, видимые 2 мм (ПВХ/АБС).
4. Номинальные зазоры: дверь купе — боковина 3 мм, фасад ящика — стойка 2 мм; ящики внутри купе — с накладкой 30 мм на стойке со стороны нахлёста дверей.
5. Ящики — направляющие полного выдвижения NL 450 (внутренняя глубина 496 мм ≥ NL + 3); присадка по 32-й системе — выполняет цех.
6. Компенсатор 20 мм — короб из ЛДСП по фронту и торцам, подгоняется к потолку при монтаже (припуск 20 мм), крепится к корпусу и к потолку.
7. Сборка стоя на месте (решение по изделию): корпус не собирается лёжа и не поднимается собранным — собирается в проектном положении у стены; траектория подъёма на виде не показана. Диагональ боковины √(2600² + 600²) = 2668 мм > 2620 мм до потолка: поднять собранный корпус нельзя.
8. Крепление к стене от опрокидывания — уголки 2 шт. к несущему основанию (монтажная схема шкафов).

## Условные обозначения

- дверь купе, стрелка — направление движения
- корпус и полки ЛДСП (вид на стену)
- задняя стенка ХДФ
- деталь в разрезе
- компенсатор — короб до потолка
- штанга для плечиков (на разрезе — плечики 450 мм)

**Допущения и предложения на листе**

Основа листа: размеры сняты со скана плана заказчика по размерным цепочкам, контрольный обмер на объекте не выполнялся (К-13); высота потолка 2700 мм принята: на плане заказчика не указана (К-11); толщины стен приняты: наружные 250 мм, перегородки 150 мм (на плане 85–190 мм) (К-13); разрешённая мощность 15 кВт принята по типовой квартире, технических условий нет (К-14); утолщение стены 190 × 1360 мм и элемент 1470 × 160 мм плана заказчика не определены (К-12); ниша санузла 2 закрыты перегородкой и фальш-стеной: проектное решение, на плане заказчика ниша у входа открыта (К-18); несущие стены не определены: до технического заключения все существующие стены считаются несущими (К-20); окна существующие и сохраняются; подоконная доска и глубина откосов не заданы — приняты, не замерены (К-27).
См. лист открытых вопросов (лист 6, запись К-11; лист 7, записи К-12–К-14, К-18, К-20; лист 8, запись К-27).

1000 мм · печать 1:1

| | | | | | | | |
|---|---|---|---|---|---|---|---|
| | | | | | | ГД-2026-003-АИ | |
| | | | | | | Трёхкомнатная квартира | |
| | | | | | | Общая площадь 78,95* м² · * размеры со скана, не замерены (реестр — п. 6–11, К-13) | |
| Изм. | Кол.уч | Лист | № док. | Подп. | Дата | Дизайн-проект интерьера трёхкомнатной квартиры | Стадия: РП; Лист: 62; Листов: 94 |
| Разраб. | | Кырпан А.С. | | | 05.10.26 | | |
| Пров. | | | | | | | |
| ГИП | | | | | | | |
| | | | | | | Шкаф-купе М16 | Кырпан Александр Сергеевич |
| Н. контр. | | | | | | | |
| Утв. | | | | | | М 1:20 | |

выпуск 05.10.2026 · 6add39ab8d · стр. 72 из 137

# Кухня (пом. 6). Развёртка гарнитура

Кухня-гостиная (пом. 6) · стена В · вид из помещения · размеры в мм, отметки в м

## Вид с фасадами

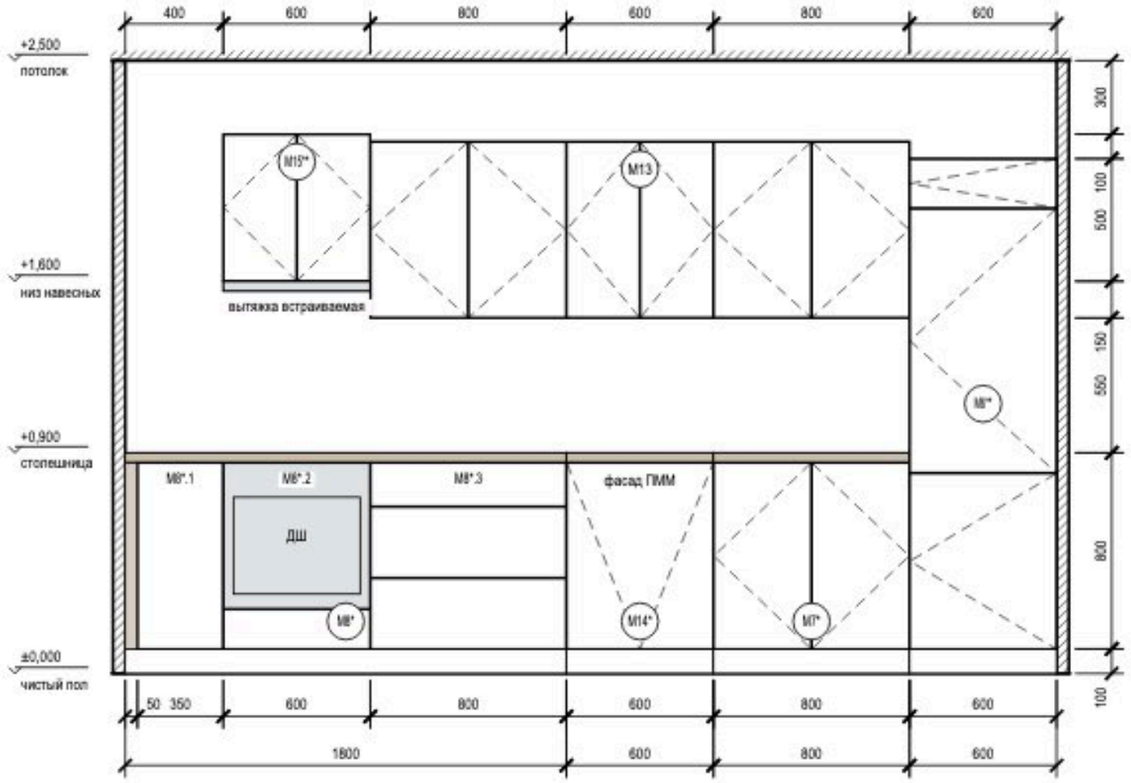


## Вид без фасадов (наполнение, выводы)

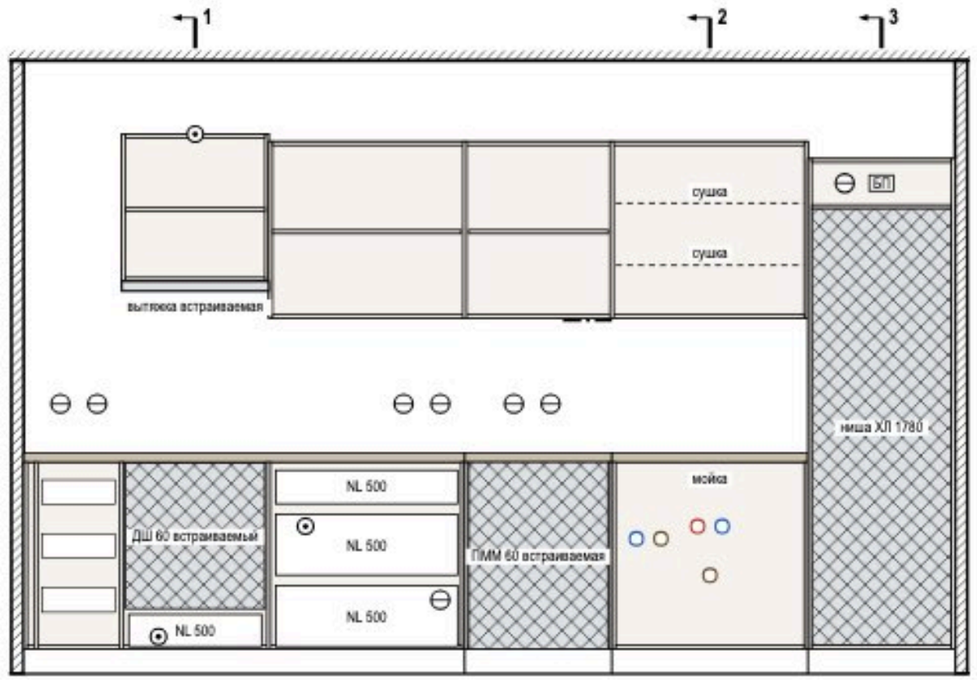


## Разрез 1-1

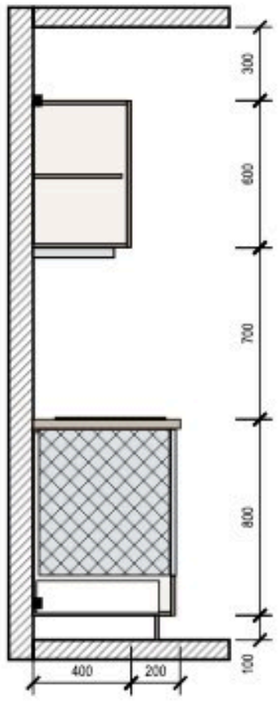


## Разрез 2-2

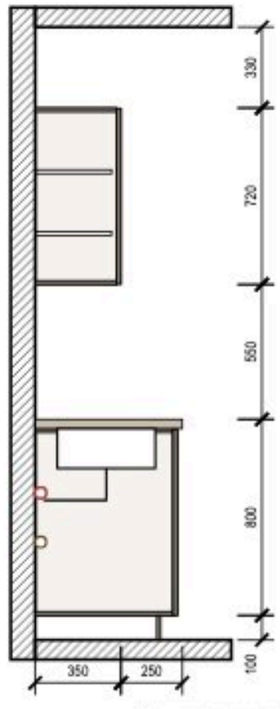


## Разрез 3-3

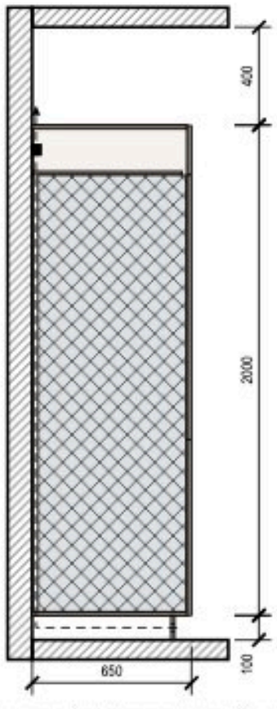


1000 мм · печать 1:1

## Условные обозначения

- фасад распашной: линии сходятся к стороне петель
- фасад ящика, карго
- встраиваемая техника
- столешница
- доборная планка
- деталь в разрезе
- К1 — марка модуля
- розетка на стене
- вывод кабеля к технике
- В1 — вывод воды В1 / Т3, канализации К1

## Примечания

1. Размеры — в мм по чистовой отделке, вид из помещения; марки — как на плане расстановки. Перед раскроем — контрольный замер цеха после фартука и пола.
2. Корпуса — ЛДСП 16 мм, задняя стенка ХДФ 4 мм; фасады — МДФ, эмаль матовая 18 мм, цвет по колерной карте; столешница 38 мм, свес 20 мм; цоколь 100 мм.
3. Кромка: скрытые торцы 0,4 мм, видимые 2 мм. Номинальные зазоры: между фасадами 3 мм, фасад — столешница 3 мм, фасад — стена не менее 3 мм.
4. Ящики полного выдвижения и петли — с доводчиком; присадка по 32-й системе — выполняет цех.
5. Вытяжка встраивается в навесной модуль над варочной; её низ 660 мм над панелью.
6. Ниши техники (холодильник — ориентир 1780 мм) — по монтажным схемам выбранных моделей: решётка в цоколе и канал за пеналом холодильника, зазор за духовым шкафом, фасад ПММ на двери машины.
7. Допущение проекта: кухня: раскладка гарнитура принята проектной, решение автора (ИЗ-12) — мойка М7* у шахты Ш2, ПММ М14* рядом с мойкой, варочная и духовой шкаф в М8*, вытяжка М15**, холодильник М6**; выводы техники — по типовой расстановке; условие: до начала черновых работ сверить раскладку и выводы с чертежом кухни от изготовителя, выводы пересматриваются по его чертежу (вопрос К-8).
8. Марки из допущений, которых нет на этом листе: Ш2 — лист 39.

Допущения и предложения на листе. Знак «*» принято (замерить). Знак «**» предложено (согласовать). См. лист открытых вопросов (листы 6–11).

| Изм. | Кол.уч | Лист | № док. | Подп. | Дата |
|---|---|---|---|---|---|
| Разраб. | | Кырпан А.С. | | | 05.10.26 |
| Пров. | | | | | |
| ГИП | | | | | |
| | | | | | |
| Н. контр. | | | | | |
| Утв. | | | | | |

**ГД-2026-003-АИ**

Трёхкомнатная квартира

Общая площадь 78,95* м² · * размеры со скана, не замерены (реестр — л. 6–11, К-13)

Дизайн-проект интерьера трёхкомнатной квартиры

| Стадия | Лист | Листов |
|---|---|---|
| РП | 63 | 94 |

Кухня (пом. 6). Развёртка гарнитура

М 1:25

Кырпан Александр Сергеевич

выпуск 05.10.2026 · 6add39ab8d · стр. 73 из 137

# Кухня (пом. 6). Монтажная схема

Кухня-гостиная (пом. 6) · стена В · размеры в мм от чистых поверхностей, высоты — от чистого пола

## Привязка выводов и крепление модулей

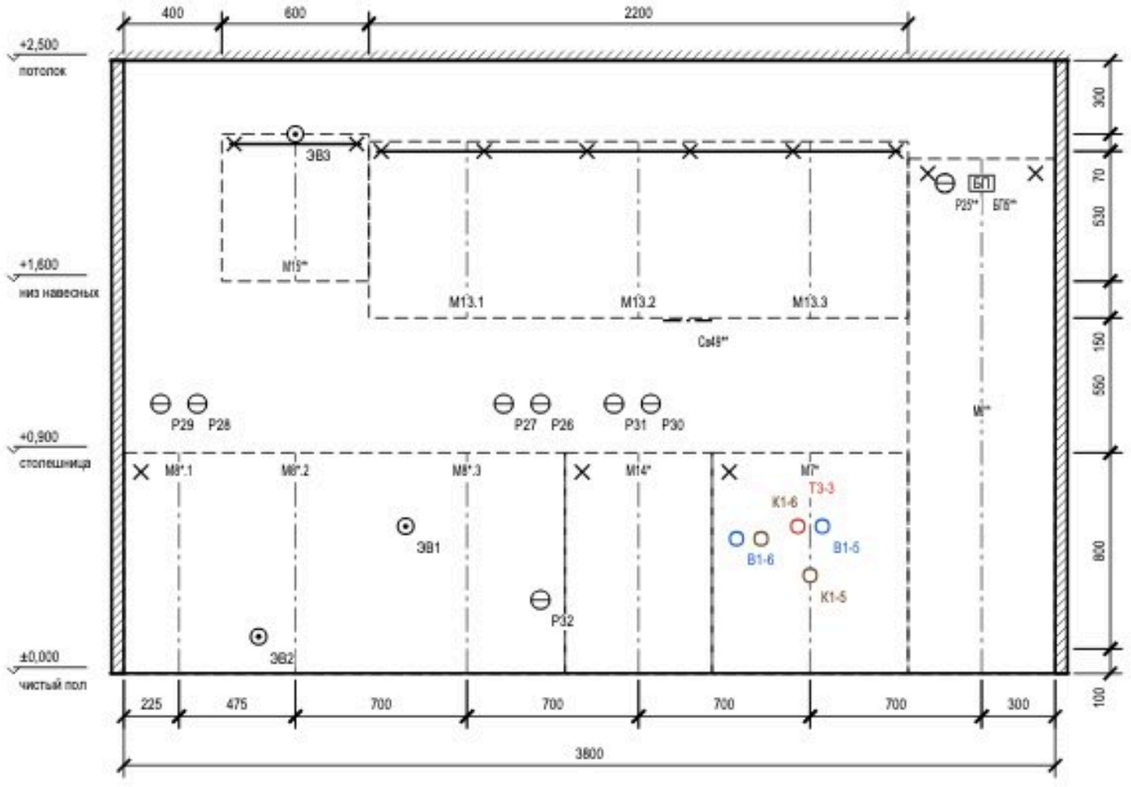


## План столешницы

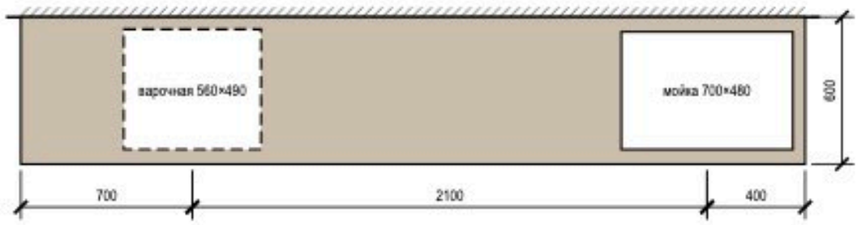


## Привязка выводов к осям модулей

| Код | Назначение | Модуль | От оси, мм | Н, мм | Размещение |
|---|---|---|---|---|---|
| Р29 | розетка — фартук | М8*.1 | −75 | 1100 | над столешницей (фартук) |
| Р28 | розетка ×2 — фартук | М8*.1 | +75 | 1100 | над столешницей (фартук) |
| ЭВ2 | вывод кабеля — духовой шкаф | М8*.2 | −150 | 150 | под духовым шкафом, доступ через ящик |
| ЭВ3 | вывод кабеля — вытяжка | М15** | 0 | 2200 | в навесном модуле |
| ЭВ1 | вывод кабеля — варочная панель (в соседнем модуле М8*.3, за ящиком) | М8*.3 | −250 | 600 | в соседнем модуле, за ящиком |
| Р27 | розетка — фартук | М8*.3 | +150 | 1100 | над столешницей (фартук) |
| Р26 | розетка ×2 — фартук | М8*.3 | +300 | 1100 | над столешницей (фартук) |
| Р32 | розетка — посудомоечная машина | М8*.3 | +300 | 300 | в соседнем модуле, за ящиком |
| Р31 | розетка — фартук между мойкой и варочной | М14* | −100 | 1100 | над столешницей (фартук) |
| Р30 | розетка ×2 — фартук между мойкой и варочной | М14* | +50 | 1100 | над столешницей (фартук) |
| Св49** | светодиодная лента — подсветка столешницы | М14* | +200 | 1440 | в профиле по низу навесного модуля |
| В1-6 | В1 — кран ПММ в шкафу мойки | М7* | −300 | 550 | в модуле мойки |
| К1-6 | К1 Ø40 — слив ПММ в шкафу мойки | М7* | −200 | 550 | в модуле мойки |
| Т3-3 | Т3 — межос. 100 | М7* | −50 | 600 | в модуле мойки |
| К1-5 | К1 Ø50 — мойка | М7* | 0 | 400 | в модуле мойки |
| В1-5 | В1 — межос. 100 | М7* | +50 | 600 | в модуле мойки |
| Р25* | розетка — холодильник, над нишей М6** (съёмная панель) | М8* | −150 | 2000 | над нишей холодильника, съёмная панель |
| БП5* | блок питания — в пенале М6**, верх, съёмная панель | М8* | 0 | 2000 | над нишей холодильника, съёмная панель |

## Зазоры под отделку

| Поверхность | Отделка | Зазор, мм | Учесть |
|---|---|---|---|
| фартук | керамогранит | 10 | от чернового основания до корпуса навесных и столешницы |
| стены | окраска | 5 | под штукатурку и шпаклёвку за пеналом |
| пол | инженерная доска | | цоколь — после укладки пола, опоры ±20 мм |

## Условные обозначения

- навесной модуль (невидимый контур)
- ось модуля (от неё — привязка вывода)
- анкер / уголок крепления к стене
- розетка на стене
- вывод кабеля к технике
- ○ В1 — вывод воды В1 / Т3, канализации К1

## Примечания

1. Выводы — по проекту электрики и ВК; привязка по горизонтали — от оси модуля (плюс — вправо по виду), по высоте — от чистого пола до оси вывода.
2. Пенал — уголки к стене 2 шт. сверху; нижние модули — стяжками между собой и уголком к стене; ряд выставить по уровню опорами цоколя.
3. Розетки над столешницей — не ниже 150 мм над ней и не за корпусом техники; розетка за ПММ, духовым шкафом и холодильником — только в соседнем модуле или в зоне цоколя с доступом.
4. Столешница — вырезы по шаблонам выбранных моделей мойки и варочной панели; торцы у стены — герметик, пристеночный плинтус.
5. Допущение проекта: кухня: раскладка гарнитура принята проектной, решение автора (ИЗ-12) — мойка М7* у шахты Ш2, ПММ М14* рядом с мойкой, варочная и духовой шкаф в М8*, вытяжка М15**, холодильник М6**; выводы техники — по типовой расстановке; условие: до начала черновых работ сверить раскладку и выводы с чертежом кухни от изготовителя, выводы пересматриваются по его чертежу (вопрос К-6).
6. Марки из допущений, которых нет на этом листе: Ш2 — лист 39.

Допущения и предложения на листе. Основа листа: размеры сняты со скана плана заказчика по размерным цепочкам, контрольный обмер на объекте не выполнялся (К-13); высота потолка 2700 мм принята: на плане заказчика не указана (К-11); толщины стен приняты: наружные 250 мм, перегородки 150 мм (на плане 85–190 мм) (К-13); разрешённая мощность 15 кВт принята по типовой квартире, технических условий нет (К-14); утолщение стены 190 × 1360 мм и элемент 1470 × 160 мм плана заказчика не определены (К-12); ниши санузла 2 закрыты перегородкой и фальш-стеной: проектное решение, на плане заказчика ниша у входа открыта (К-18); несущие стены не определены: до технического заключения все существующие стены считаются несущими (К-20); окна существующие и сохраняются; подоконная доска и глубина откосов не заданы — приняты, не замерены (К-27). Знак «*» — принято, не замерено и не подтверждено (замерить на объекте). Знак «**» — предложение проектировщика, заказчиком не утверждено (согласовать с заказчиком): ИЗ-3: Св49, БП5 — диммируемость добавлена разработчиком проекта под светорегуляторы S11 и S12; К-7, К-8: Р25 — высота 2000 мм выше нормы 1 м (ПУЭ 6.6.30) по назначению: питание встроенного холодильника М6, розетка над нишей за съёмной панелью. См. лист открытых вопросов (лист 6, записи К-7, К-8, К-11; лист 7, записи К-12–К-14, К-18, К-20; лист 8, записи К-24, К-27; лист 9, записи ИЗ-3, ИЗ-5); по листу — К-24.

1000 мм · печать 1:1

| Изм. | Кол.уч | Лист | № док. | Подп. | Дата |
|---|---|---|---|---|---|
| Разраб. | | Кырпан А.С. | | | 05.10.26 |
| Пров. | | | | | |
| ГИП | | | | | |
| | | | | | |
| Н. контр. | | | | | |
| Утв. | | | | | |

**ГД-2026-003-АИ**

Трёхкомнатная квартира

Общая площадь 78,95* м² · * размеры со скана, не замерены (реестр — п. 6–11, К-13)

Дизайн-проект интерьера трёхкомнатной квартиры

| Стадия | Лист | Листов |
|---|---|---|
| РП | 64 | 94 |

**Кухня (пом. 6). Монтажная схема**

М 1:25

Кырпан Александр Сергеевич

выпуск 05.10.2026 · 6add39ab8d · стр. 74 из 137

# Шкафы. Монтажная схема

крепление к стене, установочные размеры, зазоры под отделку · размеры в мм

**Шкаф распашной С5 (пом. 1)**

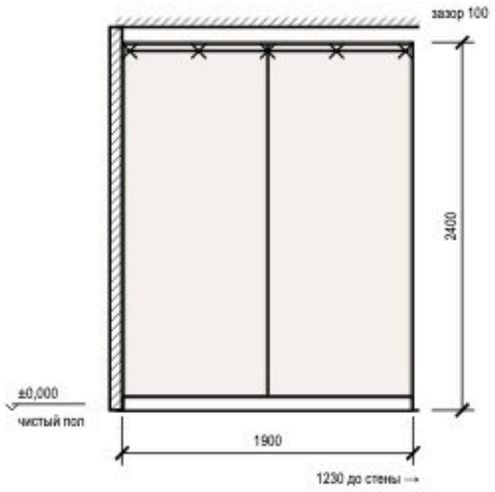


**Система хранения Г1 (пом. 3)**

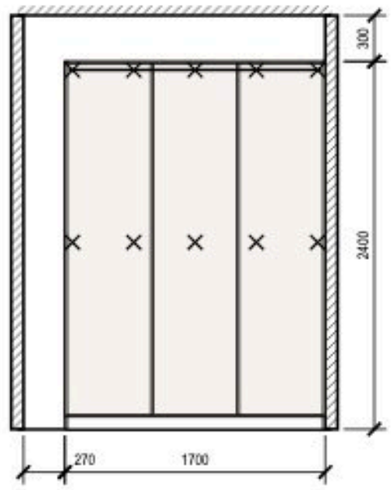


**Шкаф-купе М16 (пом. 5)**

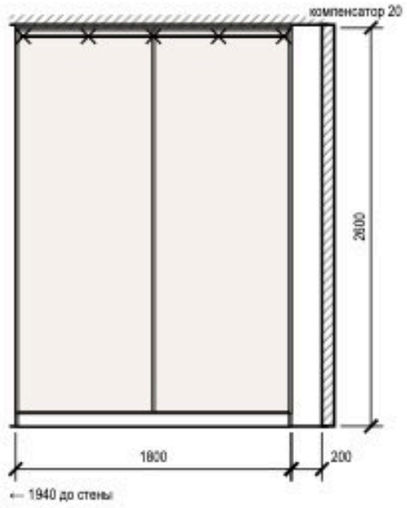


## Крепление и зазоры под отделку

| Марка | Помещение, стена | Основание | Отделка стены | Зазор, мм | Крепёж по плане | От опрокидывания |
|---|---|---|---|---|---|---|
| С5 | Спальня 1 (1), стена Б | по основанию — см. таблицу крепежа | окраска | 5 | анкер 5 шт., шаг 450 | уголок к стене, 2 шт. |
| Г1 | Гардеробная (3), стена Г | по основанию — см. таблицу крепежа | окраска | 5 | анкер 10 шт. (2 ряда) | крепление к стене, 3 точки |
| М16 | Прихожая (5), стена Г | по основанию — см. таблицу крепежа | окраска | 5 | анкер 5 шт., шаг 425 | уголки 2 шт. |

## Крепёж по основанию стены

| Основание стены | Крепёж |
|---|---|
| бетон, ж/б | анкер-шуруп 7,5×72 или дюбель 8×60 с шурупом 5×70 |
| кирпич полнотелый | дюбель 8×80 с шурупом 5×90 |
| газобетон, пазогребень | дюбель для газобетона 10×100 или химический анкер |
| гипсокартон | закладная до обшивки (брус 40×80 или фанера 18 мм), саморез в закладную |

## Условные обозначения

- × — анкер / уголок крепления к стене
- прямоугольник — корпус и полки ЛДСП (вид на стену)
- заштрихованная полоса — компенсатор — короб до потолка

## Примечания

1. Установочные размеры — от чистого пола и чистых стен; перед установкой контрольный замер после отделки.
2. Порядок: корпус выставить по уровню опорами цоколя → закрепить к стене по задней планке → навесить двери и фасады, отрегулировать зазоры → подогнать и закрепить компенсатор.
3. Анкеры — с шагом не более 500 мм, не ближе 50 мм от края планки; на ГКЛ только в закладную, установленную до обшивки.
4. Скрытые коммуникации под анкеры проверить детектором; трассы электрики по плану розеток.
5. Сборка стоя на месте: М16 (диагональ боковины 2668 мм > 2620 мм до потолка) — корпус не собирается лёжа и не поднимается собранным, а собирается в проектном положении у стены; выставление по уровню и крепление к стене выполняются по корпусу, собранному на месте.

**Допущения и предложения на листе**

Основа листа: размеры сняты со скана плана заказчика по размерным цепочкам, контрольный обмер на объекте не выполнялся (К-13); высота потолка 2700 мм принята: на плане заказчика не указана (К-11); толщины стен приняты: наружные 250 мм, перегородки 150 мм (на плане 85–190 мм) (К-13); разрешённая мощность 15 кВт принята по типовой квартире, технических условий нет (К-14); утолщение стены 190 × 1360 мм и элемент 1470 × 160 мм плана заказчика не определены (К-12); ниши санузла 2 закрыты перегородкой и фальш-стеной: проектное решение, на плане заказчика ниша у входа открыта (К-18); несущие стены не определены: до технического заключения все существующие стены считаются несущими (К-20); окна существующие и сохраняются; подоконная доска и глубина откосов не заданы — приняты, не замерены (К-27).

См. лист открытых вопросов (лист 6, запись К-11; лист 7, записи К-12–К-14, К-18, К-20; лист 8, запись К-27).

1000 мм · печать 1:1

| Изм. | Кол.уч | Лист | № док. | Подп. | Дата |
|---|---|---|---|---|---|
| Разраб. | | Кырпан А.С. | | | 05.10.26 |
| Пров. | | | | | |
| ГИП | | | | | |
| | | | | | |
| Н. контр. | | | | | |
| Утв. | | | | | |

**ГД-2026-003-АИ**

Трёхкомнатная квартира

Общая площадь 78,95* м² · * размеры со скана, не замерены (реестр — п. 6–11, К-13)

Дизайн-проект интерьера трёхкомнатной квартиры

| Стадия | Лист | Листов |
|---|---|---|
| РП | 65 | 94 |

**Шкафы. Монтажная схема**

М 1:40

Кырпан Александр Сергеевич

выпуск 05.10.2026 · 6add39ab8d · стр. 75 из 137

# Ведомости изделий, техники и фурнитуры

встроенная мебель и кухонный гарнитур · размеры в мм

## Ведомость изделий

| Марка | Наименование | Пом. | Ш×Г×В, мм | Корпус | Фасад | Кромка, мм скр./вид. | Кол. |
|---|---|---|---|---|---|---|---|
| С5 | Шкаф распашной | 1 | 1900×600×2400 | ЛДСП 16 | МДФ 18, эмаль матовая | 0,4 / 2 | 1 |
| Г1 | Система хранения | 3 | 1700×600×2400 | ЛДСП 16 | без фасадов; ящики — МДФ 18, эмаль матовая | 0,4 / 2 | 1 |
| М16 | Шкаф-купе | 5 | 1800×600×2600 | ЛДСП 16 | рифлёные панели МДФ в алюминиевом профиле | 0,4 / 2 | 1 |
| М8* | Модуль нижний: карго, духовой шкаф, ящики, варочная | 6 | 1800×600×900 | ЛДСП 16 | МДФ 18, эмаль матовая | 0,4 / 2 | 1 |
| М15** | Модуль навесной: полки | 6 | 600×400×600 | ЛДСП 16 | МДФ 18, эмаль матовая | 0,4 / 2 | 1 |
| М13 | Модуль навесной: полки, сушка | 6 | 2200×350×720 | ЛДСП 16 | МДФ 18, эмаль матовая | 0,4 / 2 | 1 |
| М14* | Модуль нижний: ПММ | 6 | 600×600×900 | ЛДСП 16 | МДФ 18, эмаль матовая | 0,4 / 2 | 1 |
| М7* | Модуль нижний: мойка | 6 | 800×600×900 | ЛДСП 16 | МДФ 18, эмаль матовая | 0,4 / 2 | 1 |
| М6** | Пенал: холодильник встр. | 6 | 600×650×2100 | ЛДСП 16 | МДФ 18, эмаль матовая | 0,4 / 2 | 1 |

## Ведомость встраиваемой техники

| Поз. | Прибор | Ниша, вырез, мм | Вентиляция | Питание | Схема |
|---|---|---|---|---|---|
| М8*.2 | Духовой шкаф встраиваемый, 60 см | ниша 560 × 595, глубина ≥ 550 | зазор за шкафом, вырез в задней стенке | вывод кабеля под шкафом | по модели |
| М8*.2 | Варочная панель индукционная, 60 см | вырез в столешнице 560 × 490 | | вывод кабеля под модулем | по модели |
| М14* | Посудомоечная машина встраиваемая, 60 см | ниша 600 × 862 (от пола до низа столешницы) | зазор в цоколе, по схеме | розетка в соседнем модуле | по модели |
| М7* | Мойка врезная / подстольная с сифоном | вырез по шаблону, ориентир 700 × 480 | | смеситель — выводы ВК | по модели |
| М6** | Холодильник встраиваемый, ниша 1780 | ниша 1780 × 560 × 550 | решётка в цоколе, канал за корпусом, выход сверху | розетка над нишей или в соседнем модуле | по модели |
| М8*.2 | Вытяжка настенная, 60 см | низ ≥ 650 над панелью | воздуховод к вентканалу, короб до потолка | вывод кабеля в коробе | по модели |

## Ведомость фурнитуры

| № | Фурнитура | Тип, размер | Изделия | Кол. |
|---|---|---|---|---|
| 1 | Петля накладная 110° с доводчиком | чашка 35 мм | С5, М15**, М13, М7*, М6** | 51 |
| 2 | Полкодержатель с фиксацией | ø5 мм | С5, Г1, М16, М15**, М13, М6** | 96 |
| 3 | Штанга овальная 30×15, L = 926 | + 2 держателя | С5 | 1 |
| 4 | Опора регулируемая с цоколем на клипсах | ход 20 мм | С5, Г1, М16 | 24 |
| 5 | Анкер по основанию стены | по таблице крепежа | С5, Г1, М16, М15**, М13 | 28 |
| 6 | Уголок крепления к стене от опрокидывания | стальной | С5, Г1, М16, М6** | 8 |
| 7 | Штанга овальная 30×15, L = 545 | + 2 держателя | Г1 | 3 |
| 8 | Система дверей купе: профиль, направляющие, ролики | на 2 двери | М16 | 1 |
| 9 | Ручка-профиль вертикальная | в цвет профиля | М16 | 2 |
| 10 | Штанга овальная 30×15, L = 876 | + 2 держателя | М16 | 1 |
| 11 | Полка для обуви выдвижная наклонная | ширина 876 | М16 | 3 |
| 12 | Карго выдвижное 3-уровневое | ширина 350 | М8* | 1 |
| 13 | Направляющие полного выдвижения с доводчиком NL 500 | пара | М8* | 4 |
| 14 | Ручка-профиль | латунь матовая | М8*, М15**, М13, М14*, М7*, М6** | 19 |
| 15 | Опора кухонная регулируемая 100–120 мм | + клипса цоколя | М8*, М14*, М7*, М6** | 20 |
| 16 | Навес регулируемый для навесного шкафа | пара на секцию | М15**, М13 | 4 |
| 17 | Шина монтажная | L = 540 | М15** | 1 |
| 18 | Сушка для посуды в шкаф | ширина 800 | М13 | 1 |
| 19 | Шина монтажная | L = 2140 | М13 | 1 |
| 20 | Комплект навески фасада ПММ | из поставки машины | М14* | 1 |

**Допущения и предложения на листе**

Основа листа: размеры сняты со скана плана заказчика по размерным цепочкам, контрольный обмер на объекте не выполнялся (К-13); высота потолка 2700 мм принята: на плане заказчика не указана (К-11); толщины стен приняты: наружные 250 мм, перегородки 150 мм (на плане 85–190 мм) (К-13); разрешённая мощность 15 кВт принята по типовой квартире, технических условий нет (К-14); утолщение стены 190 × 1360 мм и элемент 1470 × 160 мм плана заказчика не определены (К-12); ниши санузла 2 закрыты перегородкой и фальш-стеной: проектное решение, на плане заказчика ниша у входа открыта (К-18); несущие стены не определены: до технического заключения все существующие стены считаются несущими (К-20); окна существующие и сохраняются; подоконная доска и глубина откосов не заданы — приняты, не замерены (К-27).

Знак «*» — принято, не замерено и не подтверждено (замерить на объекте): К-8: М7, М14, М8.

Знак «**» — предложение проектировщика, заказчиком не утверждено (согласовать с заказчиком): ИЗ-5, К-8: М6, М15.

См. лист открытых вопросов (лист 6, записи К-8, К-11; лист 7, записи К-12–К-14, К-18, К-20; лист 8, запись К-27; лист 9, запись ИЗ-5).

## Примечания

1. Модели техники выбирает заказчик до изготовления мебели; ниши, вырезы и вентиляция — по монтажной схеме выбранной модели (условие гарантии), её номер вносится в ведомость.
2. Количество фурнитуры — по чертежам изделий; запас крепежа 5 %. Аналоги — по характеристикам (доводчик, нагрузка, ход).
3. Цвет корпусов, фасадов и профилей — по колерной карте проекта.
4. Допущение проекта: кухня: раскладка гарнитура принята проектной, решение автора (ИЗ-12) — мойка М7* у шахты Ш2, ПММ М14* рядом с мойкой, варочная и духовой шкаф в М8*, вытяжка М15**, холодильник М6**; выводы техники — по типовой расстановке; условие: до начала черновых работ сверить раскладку и выводы с чертежом кухни от изготовителя, выводы пересматриваются по его чертежу (вопрос К-8).
5. Марки из допущений, которых нет на этом листе: Ш2 — лист 39.

| | | | | | | |
|---|---|---|---|---|---|---|
| | | | | | | ГД-2026-003-АИ |
| | | | | | | Трёхкомнатная квартира |
| | | | | | | Общая площадь 78,95* м² · * размеры со скана, не замерены (реестр — п. 6–11, К-13) |
| Изм. | Кол.уч | Лист | № док. | Подп. | Дата | |
| Разраб. | | Кырпан А.С. | | | 05.10.26 | Дизайн-проект интерьера трёхкомнатной квартиры |
| Пров. | | | | | | Стадия: РП · Лист: 66 · Листов: 94 |
| ГИП | | | | | | |
| Н. контр. | | | | | | Ведомости изделий, техники и фурнитуры — М 6/м |
| Утв. | | | | | | Кырпан Александр Сергеевич |

выпуск 05.10.2026 · 6add39ab8d · стр. 76 из 137

09

# Развёртки и узлы

Кырлан Александр Сергеевич

выпуск 05.10.2026 № 6add39ab8d · стр. 77 из 137

# Реестр марок отделки и позиций альбома

Реестр марок отделки (О ↔ позиции колерной карты) и марки позиций по видам

## Реестр марок отделки альбома

| Марка | Поверхность | Материал, изделие | Цвет, код | Помещения | Колер. карта |
|---|---|---|---|---|---|
| О1 | стены | окраска, Farrow & Ball Modern Emulsion, матовая, подготовка Q3 | Farrow & Ball No. 241 «Skimming Stone» | 1, 4, 5, 6, 8 | К1 |
| О2 | акцентная стена | окраска, Farrow & Ball Modern Emulsion, матовая, подготовка Q3 | Farrow & Ball No. 30 «Hague Blue» | 1, 4, 6 | К2 |
| О3 | плинтус | плинтус МДФ, h 80 мм, аналог: плинтус МДФ под покраску 80×16 | Farrow & Ball No. 241 «Skimming Stone» | 1, 4, 5, 6, 8 | К4 |
| О4 | потолок | окраска, Tikkurila Anti-Reflex 2, глубокоматовая, подготовка Q3 | Tikkurila V503 «Winter» | 1, 3, 4, 5, 6, 8 | К3 |
| О5 | пол | инженерная доска, аналог: инженерная доска, дуб натуральный, масло, 1-полосная, 14/4 мм | | 1, 3, 4, 6, 8 | КМ1 |
| О6 | стены | облицовка плиткой, 600×1200×9 мм, аналог: керамогранит под травертин, матовый, затирка CG2WA | | 2, 7 | КМ2 |
| О7 | потолок | окраска, Tikkurila Luja 7, матовая, подготовка Q3 | Tikkurila V503 «Winter» | 2, 7 | К5 |
| О8 | пол | керамогранит, 600×600×9 мм, аналог: керамогранит ректифицированный под травертин, матовый, затирка CG2WA | | 2, 7 | КМ3 |
| О9 | стены | окраска, Tikkurila Harmony, матовая, подготовка Q3 | Tikkurila V503 «Winter» | 3 | К6 |
| О10 | плинтус | плинтус МДФ, h 80 мм, аналог: плинтус МДФ под покраску 80×16 | Tikkurila V503 «Winter» | 3 | К7 |
| О11 | пол | керамогранит, 600×1200×9 мм, аналог: керамогранит ректифицированный под травертин, матовый, затирка CG2WA | | 5 | КМ4 |
| О12 | фартук | керамогранит, 1200×600×9 мм, аналог: керамогранит под травертин, матовый, затирка CG2WA | | 6 | КМ5 |

## Марки позиций альбома по видам

| Префикс | Что обозначает, позиции | Листы |
|---|---|---|
| Д | двери: Д-1–Д-5 | 21–24 |
| ПР | проёмы без полотна (портал): ПР-1, ПР-2 | 21–24 |
| ОК | окна: ОК-1–ОК-4 | 21–24 |
| Г, М, С | мебель и оборудование: Г1, М1–М5, М6**, М7*, М8*, М13, М14*, М15**, М16, М17, С1–С11 | 25–28 |
| П | сантехнические приборы: П1–П3, П4*, П6–П8, П10**, П11*, П12*, П13** | 39–41 |
| ДК | декор (картины, зеркала, растения): ДК1–ДК9 | 1, 54–58 |
| Т | текстиль (шторы, ковры): Т1–Т19 | 1, 54–58 |
| S | выключатели: S1–S10, S11**, S12**, S13–S16 | 29–36 |
| Р | розетки: Р1–Р6, Р7**, Р8**, Р9–Р11, Р12**, Р13–Р16, Р17**, Р18**, Р19**, Р20–Р24, Р25**, Р26–Р32, Р33**, Р34 | 29–36 |
| LAN | розетки компьютерные: LAN1–LAN3 | 29–36 |
| Св | светильники: Св1–Св41, Св42**, Св43**, Св44**, Св45–Св48, Св49**, Св50–Св54 | 29–36 |
| БП | блоки питания LED: БП1–БП4, БП5** | 29–36 |

## Марки позиций альбома по видам (продолжение)

| Префикс | Что обозначает, позиции | Листы |
|---|---|---|
| ИП | извещатели: ИП1–ИП6 | 29–36 |
| ЭВ | выводы кабеля: ЭВ1–ЭВ3, ЭВ4**, ЭВ5**, ЭВ6**, ЭВ7** | 29–36 |
| КУП | электроустановочные изделия: КУП1**, КУП2** | 29–36 |
| ТВ | розетки ТВ: ТВ1, ТВ2 | 29–36 |
| ЩК, ЩС** | щиты: ЩК, ЩС** | 29–36 |
| ДФ | домофон: ДФ1 | 29–36 |
| АР | точки доступа Wi-Fi: АР1**, АР2** | 29–36 |
| Ст В1, Ст К1 | стояки (системы В1, Т3, К1): Ст В1-1*, Ст В1-2*, Ст К1-1*, Ст К1-2* | 39–41 |
| Ш | шахты и короба: Ш1, Ш2 | 21–24 |
| О | марки отделки (реестр альбома): О1–О12 | 2–5, 67–86 |
| К, КМ | позиции колерной карты: К1–К7, КМ1–КМ5 | 52, 53 |
| РО | радиаторы отопления: РО-1–РО-4 | 37, 38 |

## Примечания

1. Марка отделки О — одна на весь альбом: одна и та же отделка (материал, изделие, цвет, формат) на всех листах имеет одну марку; на развёртках и планах стоят марки этого реестра.
2. Столбец «Колер. карта» — позиции колерной карты (лист 52): К — окраска по коду цвета, КМ — материал без кода цвета; «Помещения» — номера по экспликации; количества — по ведомости отделки помещений (лист 51).
3. Марки позиций: один префикс — один вид позиций на весь альбом (двери Д, окна ОК, мебель М, сантехприборы П, декор ДК, текстиль Т, колерная карта К и КМ, радиаторы РО, розетки Р, выключатели S, светильники Св; стояки — «Ст» и система, например «Ст К1-1*»). Совпадение префиксов у разных видов — замечание к исходным данным, при выпуске исправляется в модели.

Допущения и предложения на листе. Основа листа: размеры сняты со скана плана заказчика по размерным цепочкам, контрольный обмер на объекте не выполнялся (К-13); высота потолка 2700 мм принята: на плане заказчика не указана (К-11); толщины стен приняты: наружные 250 мм, перегородки 150 мм (на плане 85–190 мм) (К-13); разрешённая мощность 15 кВт принята по типовой квартире, технических условий нет (К-14); утолщение стены 190 × 1360 мм и элемент 1470 × 160 мм плана заказчика не определены (К-12); ниши санузла 2 закрыты перегородкой и фальш-стеной: проектное решение, на плане заказчика ниша у входа открыта (К-18); несущие стены не определены: до технического заключения все существующие стены считаются несущими (К-20); окна существующие и сохраняются; подоконная доска и глубина откосов не заданы — приняты, не замерены (К-27). Знак «*» — принято, не замерено (замерить): ИЗ-11, К-19: П4. Знак «**» — предложено, не утверждено (согласовать): ИЗ-2, К-2, К-23: пол пом. 2, 7; ИЗ-3: S11, S12, Св42, Св43, Св44, Св49, БП5; ИЗ-8: ЭВ4, КУП1, ЭВ5, КУП2; ИЗ-17: АР1, АР2, ЩС; К-2, К-23: стены пом. 2, 7; К-7: Р12, Р17, Р18, Р19; К-7, К-8: Р25; К-23: пол пом. 1, 3–6, 8, плинтус пом. 1, 3–6, 8, фартук пом. 6. См. лист открытых вопросов (лист 6, записи К-2, К-7, К-8, К-11; лист 7, записи К-12–К-14, К-17–К-20; лист 8, записи К-23, К-27; лист 9, записи ИЗ-1–ИЗ-5, ИЗ-8, ИЗ-9; лист 10, записи ИЗ-11, ИЗ-15; лист 11, запись ИЗ-17).

| Изм. | Кол.уч | Лист | № док. | Подп. | Дата |
|---|---|---|---|---|---|
| Разраб. | | Кырпан А.С. | | | 05.10.26 |
| Пров. | | | | | |
| ГИП | | | | | |
| | | | | | |
| Н. контр. | | | | | |
| Утв. | | | | | |

**ГД-2026-003-АИ**

Трёхкомнатная квартира

Общая площадь 78,95* м² · * размеры со скана, не замерены (реестр — п. 6–11, К-13)

Дизайн-проект интерьера трёхкомнатной квартиры

| Стадия | Лист | Листов |
|---|---|---|
| РП | 67 | 94 |

Реестр марок отделки и позиций альбома

М 6/м

Кырпан Александр Сергеевич

выпуск 05.10.2026 · 6add39ab8d · стр. 78 из 137

# Схема расположения развёрток и узлов

План квартиры: марки развёрток по помещениям, выноски узлов, ведомость «марка → лист»

ПРЕДВАРИТЕЛЬНО · не для производства работ · открыто пунктов: 31 (реестр — л. 6–11)

## Развёртки и узлы: марка → лист

| Марка | Помещение / узел | Лист |
|---|---|---|
| А, Б | Спальня 1 (пом. 1) | 69 |
| В, Г | Спальня 1 (пом. 1) | 70 |
| А, Б | Ванная (пом. 2) | 71 |
| В, Г | Ванная (пом. 2) | 72 |
| А, В, Г | Гардеробная (пом. 3) | 73 |
| А, Б | Спальня 2 (пом. 4) | 74 |
| В, Г | Спальня 2 (пом. 4) | 75 |
| А, Б, В | Прихожая (пом. 5) | 76 |
| Г | Прихожая (пом. 5) | 77 |
| Б2 | Кухня-гостиная (пом. 6) | 78 |
| В1 | Кухня-гостиная (пом. 6) | 79 |
| А, Б1 | Кухня-гостиная (пом. 6) | 80 |
| В2, Г1, Г2 | Кухня-гостиная (пом. 6) | 81 |
| А, Б | Санузел 2 (пом. 7) | 82 |
| В, Г | Санузел 2 (пом. 7) | 83 |
| А, Б, В | Коридор (пом. 8) | 84 |
| Г | Коридор (пом. 8) | 85 |
| узел 1 | Порог 15 мм: мокрая зона — жилое помещение | 86 |
| узел 2 | Стык покрытий пола Т-профилем без перепада | 86 |
| узел 3 | Дверь скрытого монтажа в плоскости стены, плинтус | 86 |
| узел 4 | Короб стояков К1-1, В1-1 с люком и звукоизоляцией | 86 |
| узел 5 | Гидроизоляция санузла: заход на стены 200 мм, примыкание ванны | 86 |
| узел 6 | Плинтус МДФ 80×16 мм у окрашенной стены | 86 |

### Условные обозначения

- (А) — марка развёртки: буква стены, стрелка — взгляд
- выноска узла: над полкой — узел, под полкой — лист
- (1) — номер помещения, площадь м²

### Примечания

1. Развёртки — вид на стену изнутри помещения; буквы стен — одна система на весь альбом (как на листах выводов, плитки и отделки).
2. Стены без электроточек, мебели, декора и акцентной отделки развёрток не имеют: их отделка — по ведомости отделки помещений.
3. Узлы — на листе узлов; места применения — по выноскам этого листа и ведомости «марка → лист».

Допущения и предложения на листе. Знак «*» принято (замерить): Ст К1-1, Ст В1-1, Ст К1-2, Ст В1-2. См. лист открытых вопросов (листы 6–11).

1000 мм · печать 1:1

| Изм. | Кол.уч | Лист | № док. | Подп. | Дата |
|---|---|---|---|---|---|
| Разраб. | | Кырпан А.С. | | | 05.10.26 |
| Пров. | | | | | |
| ГИП | | | | | |
| | | | | | |
| Н. контр. | | | | | |
| Утв. | | | | | |

**ГД-2026-003-АИ**

Трёхкомнатная квартира

Общая площадь 78,95* м² · * размеры со скана, не замерены (реестр — п. 6–11, К-13)

Дизайн-проект интерьера трёхкомнатной квартиры

| Стадия | Лист | Листов |
|---|---|---|
| РП | 68 | 94 |

Схема расположения развёрток и узлов

М 1:50

Кырпан Александр Сергеевич

выпуск 05.10.2026 · 6add39ab8d · стр. 79 из 137

# Развёртки стен А, Б. Спальня 1 (пом. 1)

Спальня 1 (пом. 1) · вид изнутри помещения · размеры в мм, отметки в м

ПРЕДВАРИТЕЛЬНО · не для производства работ · открыто пунктов: 31 (реестр — л. 6–11)

## Развёртка стены А

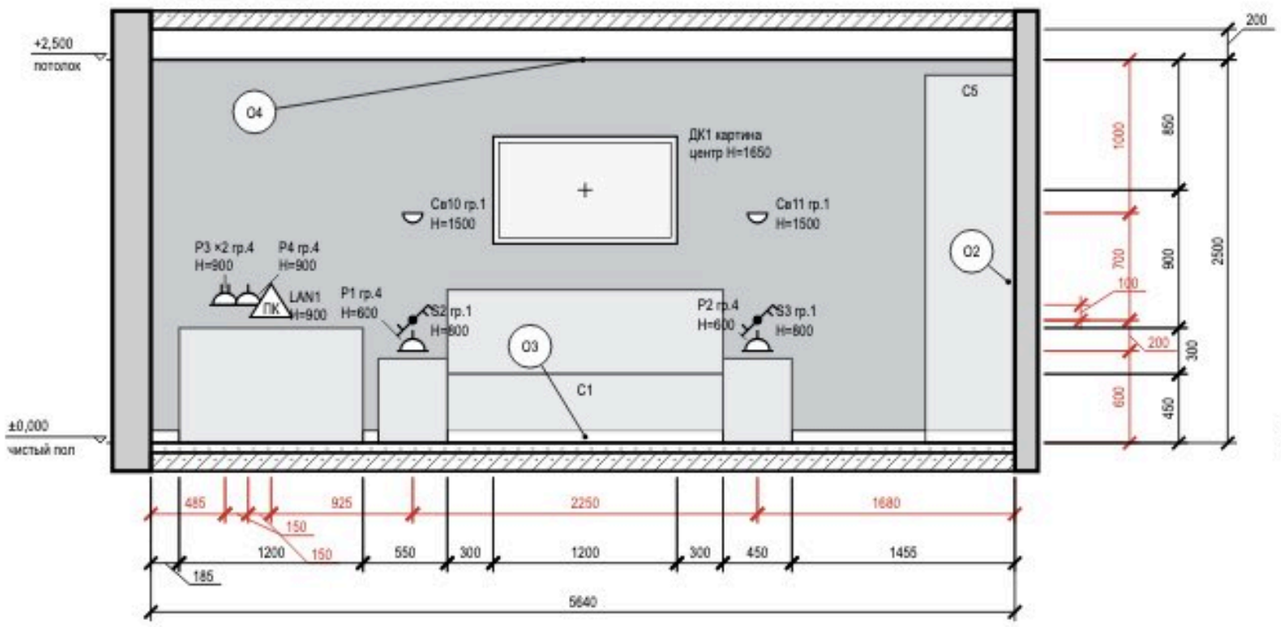


## Развёртка стены Б

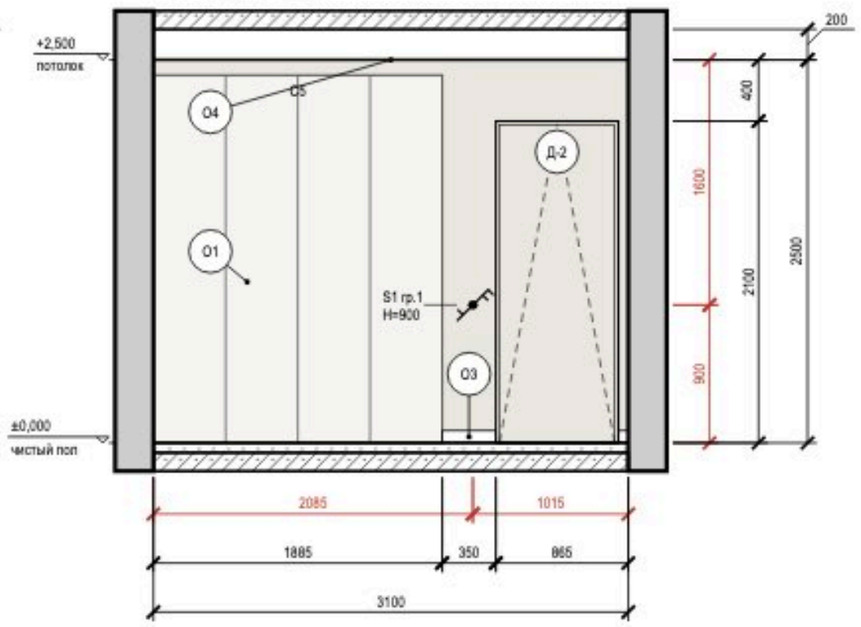


### Схема развёрток (М 1:100)

### Условные обозначения

- розетка с заземляющим контактом; у знака — марка, ×N постов в рамке, гр. — группа щита, Н — высота оси, мм
- выключатель одноклавишный
- выключатель двухклавишный (флажков — по числу клавиш)
- выключатель с проходной или перекрёстной клавишей (обратный флажок); тип клавиши — в подписи
- светильник настенный (бра), Н — высота оси
- ПК — розетка компьютерная RJ45
- привязки точек и выводов от угла и от пола, мм
- мебель и приборы — фасад по расстановке (условно)
- картина (декор): марка Д, крест — центр, Н — высота центра, мм
- дверь скрытого монтажа: полотно в плоскости стены (узел — на листе узлов)
- стены и перекрытия в сечении
- окраска: тон — цвет по коду производителя (условно)
- О1 — марка отделки по реестру отделки альбома
- А — марка развёртки: буква стены, стрелка — взгляд

### Ведомость отделки (на листе)

| Марка | Поверхность | Материал, изделие | Цвет, код | Кол. |
|---|---|---|---|---|
| О1 | стены | окраска, Farrow & Ball Modern Emulsion, матовая, подготовка Q3 | Farrow & Ball No. 241 «Skimming Stone» | 6,1 м² |
| О2 | акцентная стена | окраска, Farrow & Ball Modern Emulsion, матовая, подготовка Q3 | Farrow & Ball No. 30 «Hague Blue» | 14,1 м² |
| О3 | плинтус | плинтус МДФ, h 80 мм, аналог: плинтус МДФ под покраску 80×16 | Farrow & Ball No. 241 «Skimming Stone» | 4 м |
| О4 | потолок | окраска, Tikkurila Anti-Reflex 2, глубокоматовая, подготовка Q3 | Tikkurila V503 «Winter» | 17,8 м² |

**Допущения и предложения на листе**

Основа листа: размеры сняты со скана плана заказчика по размерным цепочкам, контрольный обмер на объекте не выполнялся (К-13); высота потолка 2700 мм принята: на плане заказчика не указана (К-11); толщины стен приняты: наружные 250 мм, перегородки 150 мм (на плане 85–190 мм) (К-13); разрешённая мощность 15 кВт принята по типовой квартире, технических условий нет (К-14); утолщение стены 190 × 1360 мм и элемент 1470 × 160 мм плана заказчика не определены (К-12); ниши санузла 2 закрыты перегородкой и фальш-стеной: проектное решение, на плане заказчика ниша у входа открыта (К-18); несущие стены не определены: до технического заключения все существующие стены считаются несущими (К-20); окна существующие и сохраняются; подоконная доска и глубина откосов не заданы — приняты, не замерены (К-27).

Знак «*» — принято, не замерено и не подтверждено (замерить на объекте): К-13: отметка существующего пола — отметка существующего пола и верха плиты не замерена: на плане заказчика отметок нет; нивелировка — в задании на обмер (К-13).

См. лист открытых вопросов (лист 6, запись К-11; лист 7, записи К-12–К-14, К-18, К-20; лист 8, запись К-27).

### Примечания

1. Развёртки — вид на стену изнутри помещения, по часовой стрелке; расположение — на схеме листа и на листе 68; размеры — в мм по чистовым поверхностям; отметки — в м от ±0,000; высоты Н — от чистого пола помещения до оси изделия, у декора — до центра.
2. Красные цепочки — привязки электроточек и выводов: по горизонтали от угла чистовых стен, по вертикали от чистого пола, до оси изделия; звенья короче 3 мм на листе вынесены во второй ярус (ближняя к стене цепочка).
3. У знака электроточки: марка (Р — розетка, S — выключатель, Св — светильник, ЭВ — вывод кабеля), ×N — число постов в рамке, гр. — группа щита, Н — высота оси от чистого пола, мм; группы по клавишам выключателя — на листе выключателей.
4. Схема мебели, приборов и декора не является технической документацией для производства мебели; габариты — по паспортам изделий.
5. Картины и зеркала крепить к основанию по паспорту изделия (закладные и анкеры — в перечне скрытых работ); крест — ось центра предмета.
6. Двери скрытого монтажа — полотно в плоскости стены, отделка стены по полотну, плинтус прерывается у короба (узел — на листе узлов).
7. Потолок на развёртках — по нижнему уровню У1; другие уровни потолка помещения: У2 +2,600.

1000 мм · печать 1:1

| Изм. | Кол.уч | Лист | № док. | Подп. | Дата |
|---|---|---|---|---|---|
| Разраб. | | Кырпан А.С. | | | 05.10.26 |
| Пров. | | | | | |
| ГИП | | | | | |
| | | | | | |
| Н. контр. | | | | | |
| Утв. | | | | | |

**ГД-2026-003-АИ**

Трёхкомнатная квартира

Общая площадь 78,95* м² · * размеры со скана, не замерены (реестр — п. 6–11, К-13)

| Дизайн-проект интерьера трёхкомнатной квартиры | Стадия | Лист | Листов |
|---|---|---|---|
| | РП | 69 | 94 |
| **Развёртки стен А, Б. Спальня 1 (пом. 1)** М 1:40 | **Кырпан Александр Сергеевич** | | |

выпуск 05.10.2026 · 6add39ab8d · стр. 80 из 137

# Развёртки стен В, Г. Спальня 1 (пом. 1)

Спальня 1 (пом. 1) · вид изнутри помещения · размеры в мм, отметки в м

ПРЕДВАРИТЕЛЬНО · не для производства работ · открыто пунктов: 31 (реестр — л. 6–11)

**Развёртка стены В**

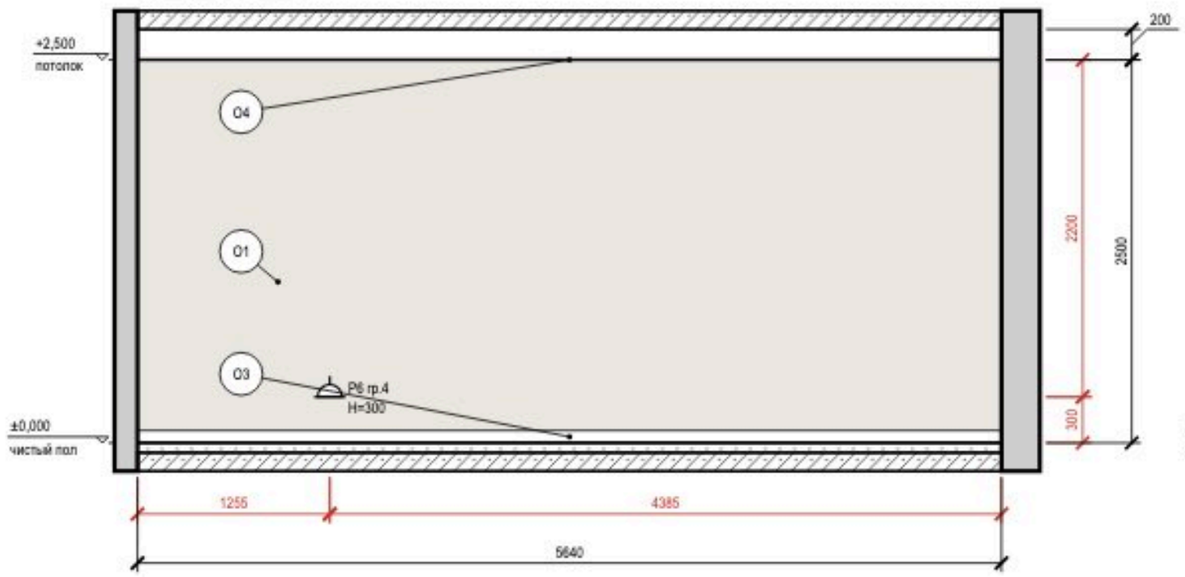


**Развёртка стены Г**

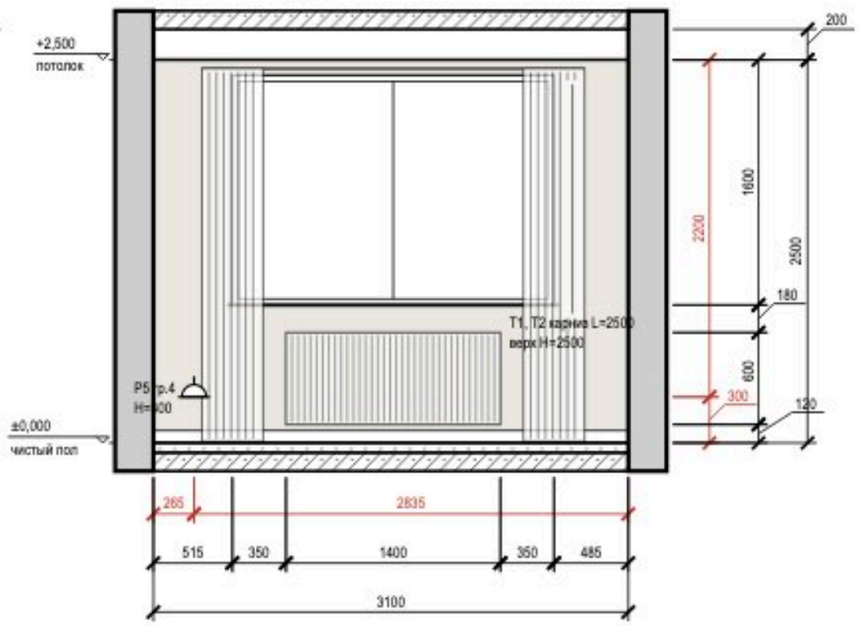


**Схема развёрток (М 1:100)**

**Условные обозначения**

- розетка с заземляющим контактом; у знака — марка, ×N постов в рамке, гр. — группа щита, Н — высота оси, мм
- привязки точек и выводов от угла и от пола, мм
- мебель и приборы — фасад по расстановке (условно)
- карниз (шина) и шторы в собранном виде: марка Т, длина L, верх Н
- окно: проём, рама, подоконник
- радиатор отопления; марка — по плану отопления
- стены и перекрытия в сечении
- окраска: тон — цвет по коду производителя (условно)
- О1 — марка отделки по реестру отделки альбома
- А — марка развёртки: буква стены, стрелка — взгляд

**Ведомость отделки (на листе)**

| Марка | Поверхность | Материал, изделие | Цвет, код | Кол. |
|---|---|---|---|---|
| О1 | стены | окраска, Farrow & Ball Modern Emulsion, матовая, подготовка Q3 | Farrow & Ball No. 241 «Skimming Stone» | 18,7 м² |
| О3 | плинтус | плинтус МДФ, h 80 мм, аналог: плинтус МДФ под покраску 80×16 | Farrow & Ball No. 241 «Skimming Stone» | 8,7 м |
| О4 | потолок | окраска, Tikkurila Anti-Reflex 2, глубокоматовая, подготовка Q3 | Tikkurila V503 «Winter» | 17,8 м² |

**Допущения и предложения на листе**

Основа листа: размеры сняты со скана плана заказчика по размерным цепочкам, контрольный обмер на объекте не выполнялся (К-13); высота потолка 2700 мм принята: на плане заказчика не указана (К-11); толщины стен приняты: наружные 250 мм, перегородки 150 мм (на плане 85–190 мм) (К-13); разрешённая мощность 15 кВт принята по типовой квартире, технических условий нет (К-14); утолщение стены 190 × 1360 мм и элемент 1470 × 160 мм плана заказчика не определены (К-12); ниши санузла 2 закрыты перегородкой и фальш-стеной: проектное решение, на плане заказчика ниша у входа открыта (К-18); несущие стены не определены: до технического заключения все существующие стены считаются несущими (К-20); окна существующие и сохраняются; подоконная доска и глубина откосов не заданы — приняты, не замерены (К-27).

Знак «*» — принято, не замерено и не подтверждено (замерить на объекте): К-13: отметка существующего пола — отметка существующего пола и верха плиты не замерена: на плане заказчика отметок нет; нивелировка — в задании на обмер (К-13).

См. лист открытых вопросов (лист 6, запись К-11; лист 7, записи К-12–К-14, К-18, К-20; лист 8, запись К-27).

**Примечания**

1. Развёртки — вид на стену изнутри помещения, по часовой стрелке; расположение — на схеме листа и на листе 68; размеры — в мм по чистовым поверхностям; отметки — в м от ±0,000; высоты Н — от чистого пола помещения до оси изделия, у декора — до центра.
2. Красные цепочки — привязки электроточек и выводов: по горизонтали от угла чистовых стен, по вертикали от чистого пола, до оси изделия; звенья короче 3 мм на листе вынесены во второй ярус (ближняя к стене цепочка).
3. У знака электроточки: марка (Р — розетка, S — выключатель, Св — светильник, ЭВ — вывод кабеля), ×N — число постов в рамке, гр. — группа щита, Н — высота оси от чистого пола, мм; группы по клавишам выключателя — на листе выключателей.
4. Схема мебели, приборов и декора не является технической документацией для производства мебели; габариты — по паспортам изделий.
5. Карнизы (шины) — по ведомости текстиля декоратора; длина L и верх Н — по развёртке, крепление — до окраски потолка.
6. Потолок на развёртках — по нижнему уровню У1; другие уровни потолка помещения: У2 +2,600.
7. Линии узора (швы плитки, складки штор, рёбра радиаторов) прерываются у знаков и выносок — просвет между линиями не менее 0,7 мм.

1000 мм · печать 1:1

| Изм. | Кол.уч | Лист | № док. | Подп. | Дата |
|---|---|---|---|---|---|
| Разраб. | | Кырпан А.С. | | | 05.10.26 |
| Пров. | | | | | |
| ГИП | | | | | |
| | | | | | |
| Н. контр. | | | | | |
| Утв. | | | | | |

**ГД-2026-003-АИ**

Трёхкомнатная квартира

Общая площадь 78,95* м² · * размеры со скана, не замерены (реестр — п. 6–11, К-13)

Дизайн-проект интерьера трёхкомнатной квартиры

| Стадия | Лист | Листов |
|---|---|---|
| РП | 70 | 94 |

Развёртки стен В, Г. Спальня 1 (пом. 1)

М 1:40

Кырпан Александр Сергеевич

выпуск 05.10.2026 · 6add39ab8d · стр. 81 из 137

# Развёртки стен А, Б. Ванная (пом. 2)

Ванная (пом. 2) · вид изнутри помещения · размеры в мм, отметки в м



## Развёртка стены А

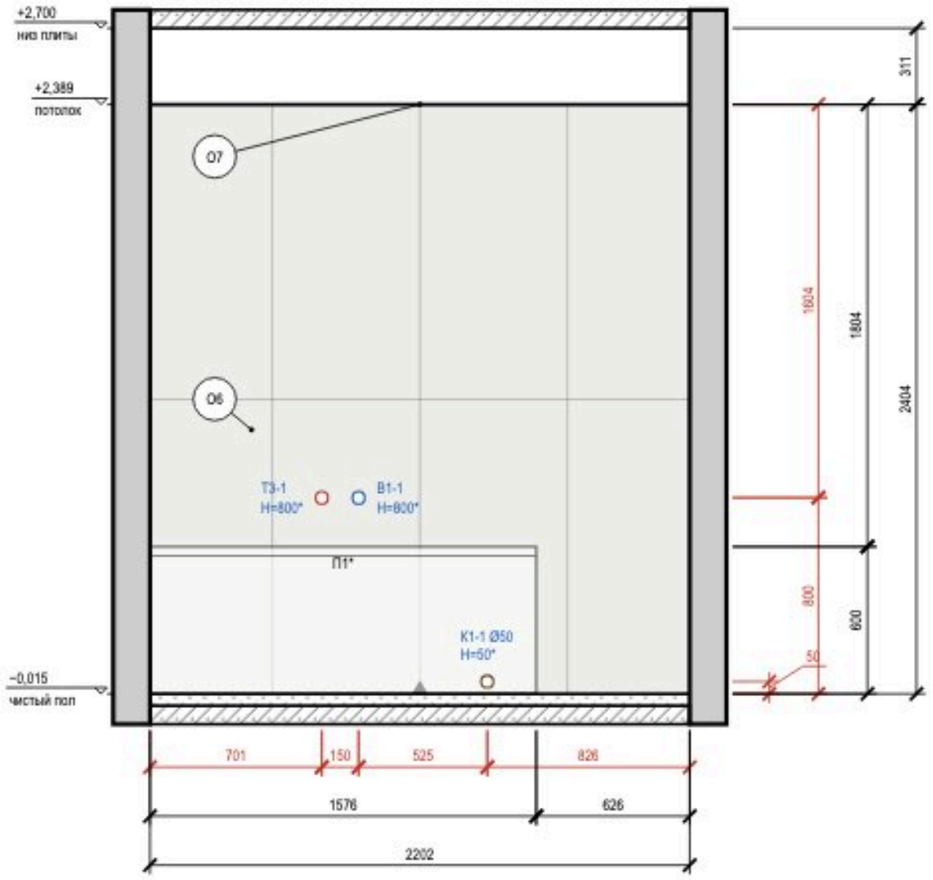


## Развёртка стены Б

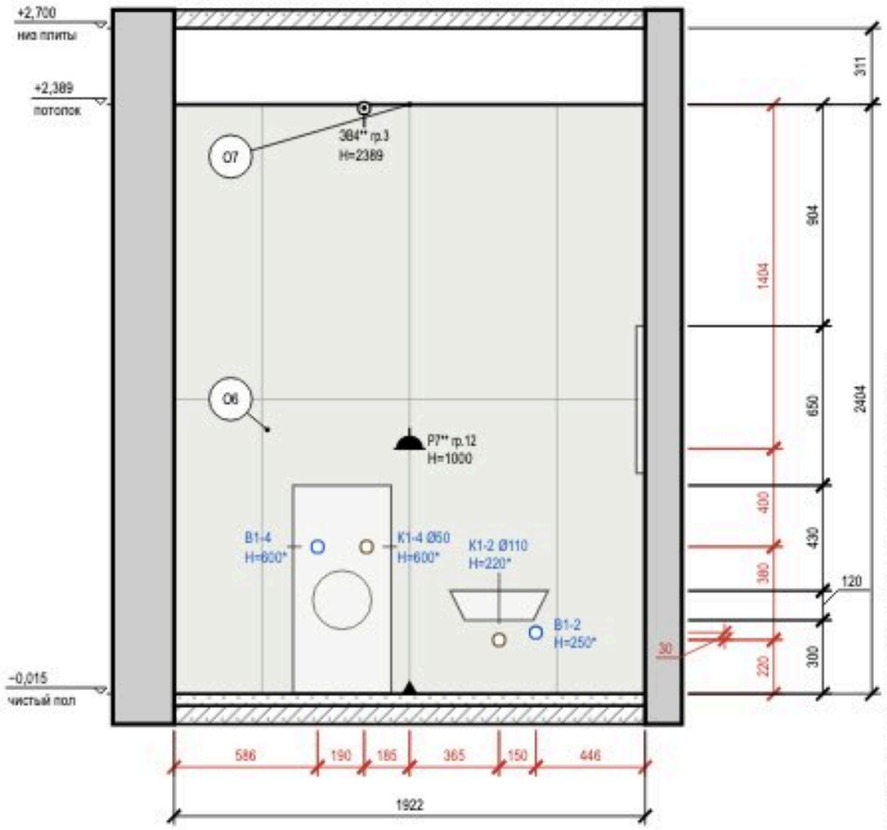


## Схема развёрток (М 1:100)

**Допущения и предложения на листе**

Основа листа: размеры сняты со скана плана заказчика по размерным цепочкам, контрольный обмер на объекте не выполнялся (К-13); высота потолка 2700 мм принята: на плане заказчика не указана (К-11); толщины стен приняты: наружные 250 мм, перегородки 150 мм (на плане 85–190 мм) (К-13); разрешённая мощность 15 кВт принята по типовой квартире, технических условий нет (К-14); утолщение стены 190 × 1360 мм и элемент 1470 × 160 мм плана заказчика не определены (К-12); ниши санузла 2 закрыты перегородкой и фальш-стенкой: проектное решение, на плане заказчика ниша у входа открыта (К-18); несущие стены не определены: до технического заключения все существующие стены считаются несущими (К-20); окна существующие и сохраняются; подоконная доска и глубина откосов не заданы — приняты, не замерены (К-27).

Знак «*» — принято, не замерено и не подтверждено (замерить на объекте): К-13: отметка существующего пола — отметка существующего пола и верха плиты не замерена: на плане заказчика отметок нет; нивелировка — в заданиях на обмер (К-13).

Знак «**» — предложение проектировщика, заказчиком не утверждено (согласовать с заказчиком): ИЗ-8: ЭВ4 — вывод к бытовому вентилятору, таймер выбега; ИЗ-9, ИЗ-15, К-7: Р7.

См. лист открытых вопросов (лист 6, записи К-7, К-11; лист 7, записи К-12–К-14, К-18, К-20; лист 8, запись К-27; лист 9, записи ИЗ-8, ИЗ-9; лист 10, запись ИЗ-15).

## Условные обозначения

- розетка влагозащищённая IP44
- вывод кабеля для подключения прибора (без розетки), марка ЭВ
- вывод В1 (код — в ведомости привязок)
- вывод Т3 (код — в ведомости привязок)
- вывод К1 (код — в ведомости привязок)
- привязки точек и выводов от угла и от пола, мм
- мебель и приборы — фасад по расстановке (условно)
- стены и перекрытия в сечении
- плитка: сетка швов по формату, ▲ — ось старта
- О1 — марка отделки по реестру отделки альбома
- А — марка развёртки: буква стены, стрелка — взгляд

## Ведомость отделки (на листе)

| Марка | Поверхность | Материал, изделие | Цвет, код | Кол. |
|---|---|---|---|---|
| О6 | стены | облицовка плиткой, 600×1200×9 мм, аналог: керамогранит под травертин, матовый, затирка CG2WA | | 9,9 м² |
| О7 | потолок | окраска, Tikkurila Luja 7, матовая, подготовка Q3 | Tikkurila V503 «Winter» | 4,4 м² |

## Примечания

1. Развёртки — вид на стену изнутри помещения, по часовой стрелке; расположение — на схеме листа и на листе 68; размеры — в мм по чистовым поверхностям; отметки — в м от ±0,000; высоты Н — от чистого пола помещения до оси изделия, у декора — до центра.
2. Красные цепочки — привязки электроточек и выводов: по горизонтали от угла чистовых стен, по вертикали от чистого пола, до оси изделия; звенья короче 3 мм на листе вынесены во второй ярус (ближняя к стене цепочка).
3. У знака электроточки: марка (Р — розетка, S — выключатель, Св — светильник, ЭВ — вывод кабеля), ×N — число постов в рамке, гр. — группа щита, Н — высота оси от чистого пола, мм; группы по клавишам выключателя — на листе выключателей.
4. Схема мебели, приборов и декора не является технической документацией для производства мебели; габариты — по паспортам изделий (* — высота не задана в проекте, показана по типовому изделию).
5. Выводы ВК — коды и высоты по листу выводов сантехники; * — высота принята по типовой практике монтажа, окончательно — по паспорту прибора.
6. Облицовка — по сетке швов 2 мм, раскладка от оси стены (треугольник у пола), целые ряды от пола; подрезки — по листу раскладки плитки.
7. Гидроизоляция в 2 слоя, заход на стены 200 мм — до облицовки, с актом скрытых работ и тестом проливом (узел — на листе узлов).

1000 мм · печать 1:1

| Изм. | Кол.уч | Лист | № док. | Подп. | Дата | ГД-2026-003-АИ | | | |
|---|---|---|---|---|---|---|---|---|---|
| | | | | | | Трёхкомнатная квартира | | | |
| | | | | | | Общая площадь 78,95* м² · * размеры со скана, не замерены (реестр — п. 6–11, К-13) | | | |
| Разраб. | | Кырпан А.С. | | | 05.10.26 | Дизайн-проект интерьера трёхкомнатной квартиры | Стадия | Лист | Листов |
| Пров. | | | | | | | РП | 71 | 94 |
| ГИП | | | | | | | | | |
| | | | | | | Развёртки стен А, Б. Ванная (пом. 2) | Кырпан Александр Сергеевич | | |
| Н. контр. | | | | | | | | | |
| Утв. | | | | | | М 1:25 | | | |

выпуск 05.10.2026 · 6add39ab8d · стр. 82 из 137

# Развёртки стен В, Г. Ванная (пом. 2)

Ванная (пом. 2) · вид изнутри помещения · размеры в мм, отметки в м

ПРЕДВАРИТЕЛЬНО · не для производства работ · открыто пунктов: 31 (реестр — л. 6–11)

## Развёртка стены В

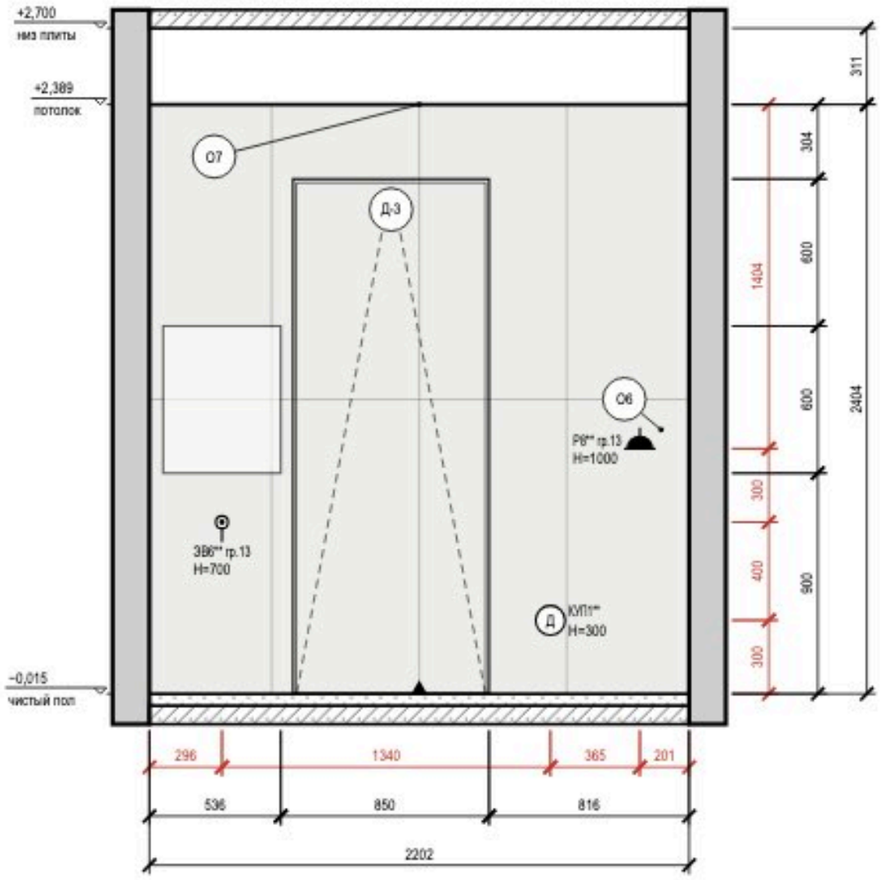


## Развёртка стены Г

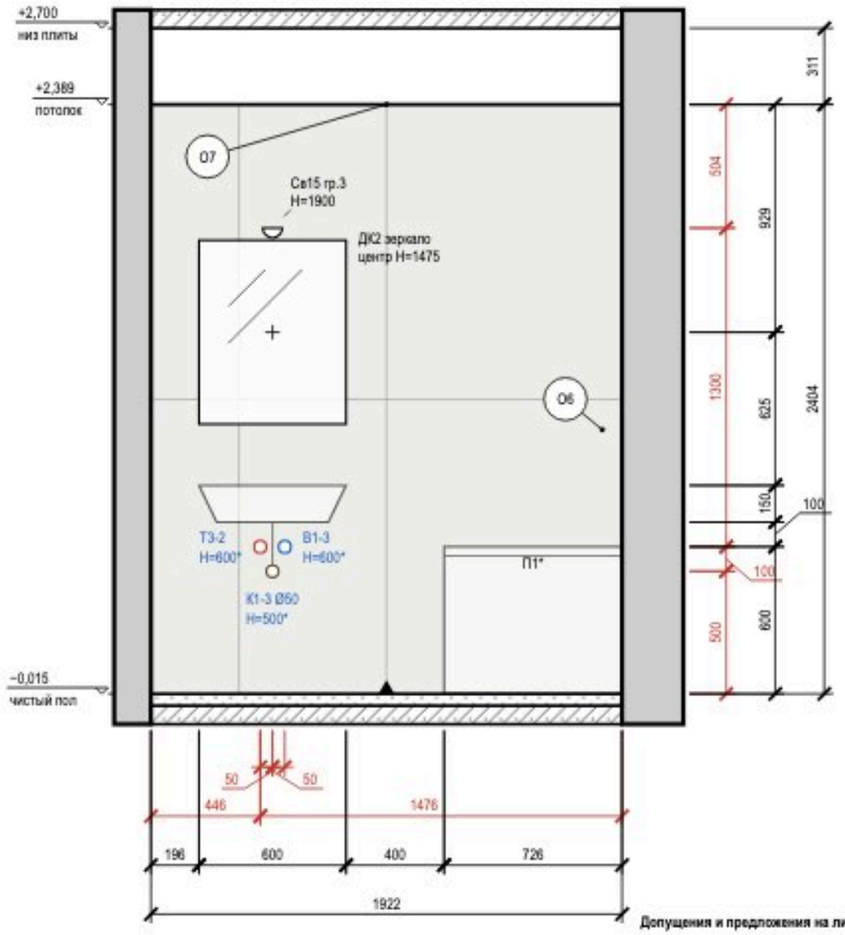


## Условные обозначения

- розетка влагозащищённая IP44
- вывод кабеля для подключения прибора (без розетки), марка ЭВ
- светильник настенный (бра), Н — высота оси
- вывод В1 (код — в ведомости привязок)
- вывод Т3 (код — в ведомости привязок)
- вывод К1 (код — в ведомости привязок)
- привязки точек и выводов от угла и от пола, мм
- мебель и приборы — фасад по расстановке (условно)
- зеркало: марка Д, крест — центр, Н — высота центра, мм
- дверь скрытого монтажа: полотно в плоскости стены (узел — на листе узлов)
- стены и перекрытия в сечении
- плитка: сетка швов по формату, ▲ — ось старта
- О1 — марка отделки по реестру отделки альбома
- А — марка развёртки: буква стены, стрелка — взгляд

## Схема развёрток (М 1:100)

## Ведомость отделки (на листе)

| Марка | Поверхность | Материал, изделие | Цвет, код | Кол. |
|---|---|---|---|---|
| О6 | стены | облицовка плиткой, 600×1200×9 мм, аналог: керамогранит под травертин, матовый, затирка CG2WA | | 8,2 м² |
| О7 | потолок | окраска, Tikkurila Luja 7, матовая, подготовка Q3 | Tikkurila V503 «Winter» | 4,4 м² |

## Примечания

1. Развёртки — вид на стену изнутри помещения, по часовой стрелке; расположение — на схеме листа и на листе 68; размеры — в мм по чистовым поверхностям; отметки — в м от ±0,000; высоты Н — от чистого пола помещения до оси изделия, у декора — до центра.
2. Красные цепочки — привязки электроточек и выводов: по горизонтали от угла чистовых стен, по вертикали от чистого пола, до оси изделия; звенья короче 3 мм на листе вынесены во второй ярус (ближняя к стене цепочка).
3. У знака электроточки: марка (Р — розетка, S — выключатель, Св — светильник, ЭВ — вывод кабеля), ×N — число постов в рамке, гр. — группа щита, Н — высота оси от чистого пола, мм; группы по клавишам выключателя — на листе выключателей.
4. Схема мебели, приборов и декора не является технической документацией для производства мебели; габариты — по паспортам изделий (* — высота не задана в проекте, показана по типовому изделию).
5. Выводы ВК — коды и высоты по листу выводов сантехники; * — высота принята по типовой практике монтажа, окончательно — по паспорту прибора.
6. Облицовка — по сетке швов 2 мм, раскладка от оси стены (треугольник у пола), целые ряды от пола; подрезки — по листу раскладки плитки.
7. Гидроизоляция в 2 слоя, заход на стены 200 мм — до облицовки, с актом скрытых работ и тестом проливом (узел — на листе узлов).
8. Картины и зеркала крепить к основанию по паспорту изделия (закладные и анкеры — в перечне скрытых работ); крест — ось центра предмета.
9. Двери скрытого монтажа — полотно в плоскости стены, отделка стены по полотну, плинтус прерывается у короба (узел — на листе узлов).

1000 мм · печать 1:1

## Допущения и предложения на листе

Основа листа: размеры сняты со скана плана заказчика по размерным цепочкам, контрольный обмер на объекте не выполнялся (К-13); высота потолка 2700 мм принята: на плане заказчика не указана (К-11); толщины стен приняты: наружные 250 мм, перегородки 150 мм (на плане 85–190 мм) (К-13); разрешённая мощность 15 кВт принята по типовой квартире, технических условий нет (К-14); уполщение стены 190 × 1360 мм и элемент 1470 × 160 мм плана заказчика не определены (К-12); ниши санузла 2 закрыты перегородкой и фальш-стеной: проектное решение, на плане заказчика ниша у входа открыта (К-18); несущие стены не определены: до технического заключения все существующие стены считаются несущими (К-20); окна существующие и сохраняются; подоконная доска и глубина откосов не заданы — приняты, не замерены (К-27).

Знак «*» — принято, не замерено и не подтверждено (замерить на объекте): К-13: отметка существующего пола — отметка существующего пола и верха плиты не замерена: на плане заказчика отметок нет; нивелировка — в задании на обмер (К-13).

Знак «**» — предложение проектировщика, заказчиком не утверждено (согласовать с заказчиком): ИЗ-1: ЭВ6; ИЗ-8: КУП1 — коробка уравнивания потенциалов, проводник от шины РЕ; ИЗ-9, К-7: Р8.

См. лист открытых вопросов (лист 6, записи К-7, К-11; лист 7, записи К-12–К-14, К-18, К-20; лист 8, запись К-27; лист 9, записи ИЗ-1, ИЗ-8, ИЗ-9).

| Изм. | Кол.уч | Лист | № док. | Подп. | Дата |
|---|---|---|---|---|---|
| Разраб. | | Кырпан А.С. | | | 05.10.26 |
| Пров. | | | | | |
| ГИП | | | | | |
| | | | | | |
| Н. контр. | | | | | |
| Утв. | | | | | |

**ГД-2026-003-АИ**

Трёхкомнатная квартира

Общая площадь 78,95* м² · * размеры со скана, не замерены (реестр — п. 6–11, К-13)

Дизайн-проект интерьера трёхкомнатной квартиры

| Стадия | Лист | Листов |
|---|---|---|
| РП | 72 | 94 |

Развёртки стен В, Г. Ванная (пом. 2)

М 1:25

Кырпан Александр Сергеевич

выпуск 05.10.2026 · 6add39ab8d · стр. 83 из 137

# Развёртки стен. Гардеробная (пом. 3)

ПРЕДВАРИТЕЛЬНО · не для производства работ · открыто пунктов: 31 (реестр — л. 6–11)

Гардеробная (пом. 3) · вид изнутри помещения · размеры в мм, отметки в м

### Развёртка стены А

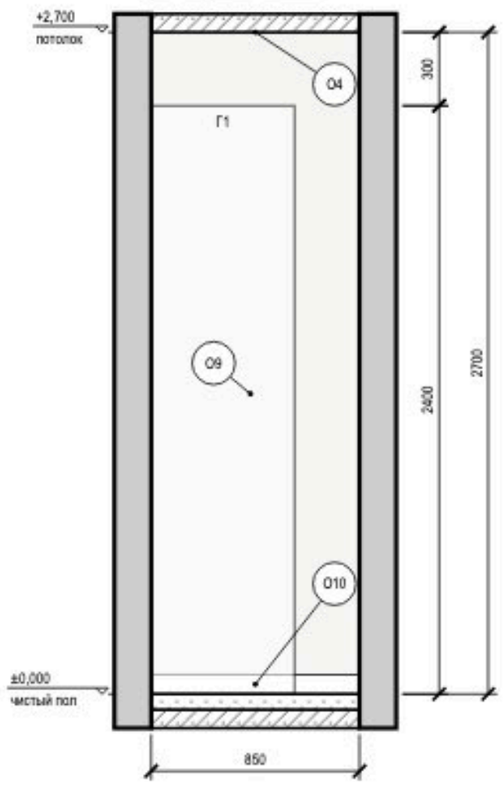


### Развёртка стены В

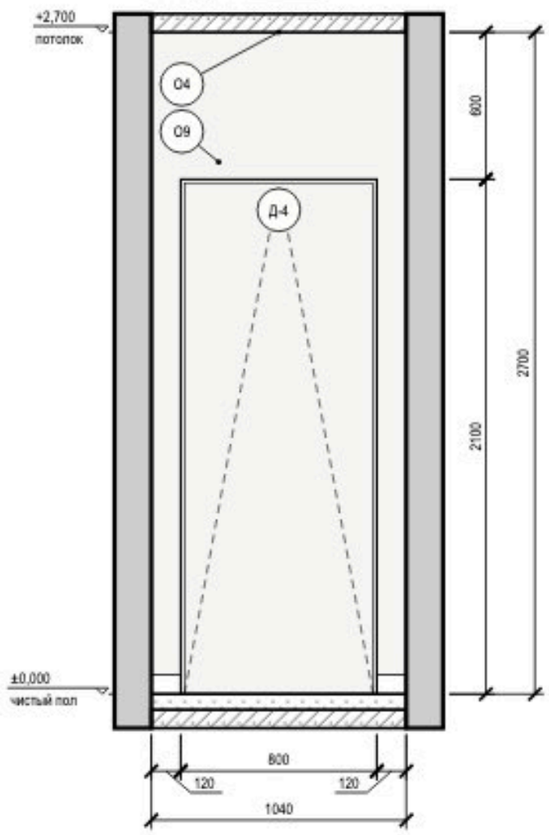


### Развёртка стены Г

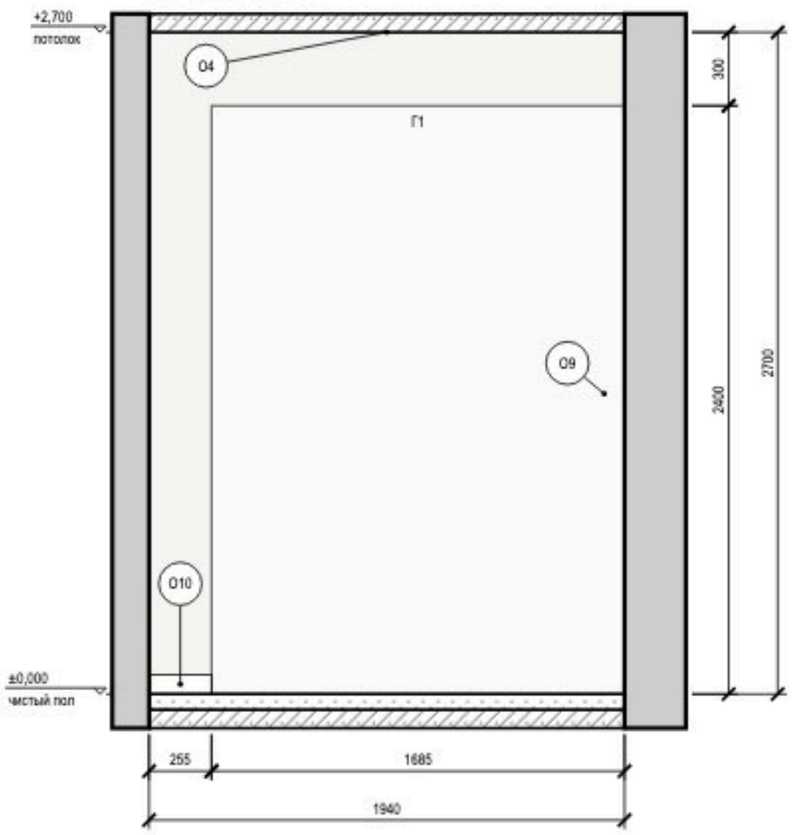


### Схема развёрток (М 1:100)

## Условные обозначения

- привязки точек и выводов от угла и от пола, мм
- мебель и приборы — фасад по расстановке (условно)
- дверь скрытого монтажа: полотно в плоскости стены (узел — на листе узлов)
- стены и перекрытия в сечении
- окраска: тон — цвет по коду производителя (условно)
- О1 — марка отделки по реестру отделки альбома
- А — марка развёртки: буква стены, стрелка — взгляд

## Ведомость отделки (на листе)

| Марка | Поверхность | Материал, изделие | Цвет, код | Кол. |
|---|---|---|---|---|
| О4 | потолок | окраска, Tikkurila Anti-Reflex 2, глубокоматовая, подготовка Q3 | Tikkurila V503 «Winter» | 1,9 м² |
| О9 | стены | окраска, Tikkurila Harmony, матовая, подготовка Q3 | Tikkurila V503 «Winter» | 8,7 м² |
| О10 | плинтус | плинтус МДФ, h 80 мм, аналог: плинтус МДФ под покраску 80×16 | Tikkurila V503 «Winter» | 1,3 м |

**Допущения и предложения на листе**

Основа листа: размеры сняты со скана плана заказчика по размерным цепочкам, контрольный обмер на объекте не выполнялся (К-13); высота потолка 2700 мм принята: на плане заказчика не указана (К-11); толщины стен приняты: наружные 250 мм, перегородки 150 мм (на плане 85–190 мм) (К-13); разрешённая мощность 15 кВт принята по типовой квартире, технических условий нет (К-14); утолщение стены 190 × 1360 мм и элемент 1470 × 160 мм плана заказчика не определены (К-12); ниши санузла 2 закрыты перегородкой и фальш-стеной: проектное решение, на плане заказчика ниша у входа открыта (К-18); несущие стены не определены: до технического заключения все существующие стены считаются несущими (К-20); окна существующие и сохраняются; подоконная доска и глубина откосов не заданы — приняты, не замерены (К-27).

Знак «*» — принято, не замерено и не подтверждено (замерить на объекте): К-13: отметка существующего пола — отметка существующего пола и верха плиты не замерена: на плане заказчика отметок нет; нивелировка — в задании на обмер (К-13).

См. лист открытых вопросов (лист 6, запись К-11; лист 7, записи К-12–К-14, К-18, К-20; лист 8, запись К-27).

## Примечания

1. Развёртки — вид на стену изнутри помещения, по часовой стрелке; расположение — на схеме листа и на листе 68; размеры — в мм по чистовым поверхностям; отметки — в м от ±0,000; высоты Н — от чистого пола помещения до оси изделия, у декора — до центра.
2. Красные цепочки — привязки электроточек и выводов: по горизонтали от угла чистовых стен, по вертикали от чистого пола, до оси изделия; звенья короче 3 мм на листе вынесены во второй ярус (ближняя к стене цепочка).
3. У знака электроточки: марка (Р — розетка, S — выключатель, Св — светильник, ЭВ — вывод кабеля), ×N — число постов в рамке, гр. — группа щита, Н — высота оси от чистого пола, мм; группы по клавишам выключателя — на листе выключателей.
4. Схема мебели, приборов и декора не является технической документацией для производства мебели; габариты — по паспортам изделий.
5. Двери скрытого монтажа — полотно в плоскости стены, отделка стены по полотну, плинтус прерывается у короба (узел — на листе узлов).

1000 мм · печать 1:1

| Изм. | Кол.уч | Лист | № док. | Подп. | Дата |
|---|---|---|---|---|---|
| Разраб. | | Кырпан А.С. | | | 05.10.26 |
| Пров. | | | | | |
| ГИП | | | | | |
| | | | | | |
| Н. контр. | | | | | |
| Утв. | | | | | |

**ГД-2026-003-АИ**

Трёхкомнатная квартира

Общая площадь 78,95* м² · * размеры со скана, не замерены (реестр — п. 6–11, К-13)

| Дизайн-проект интерьера трёхкомнатной квартиры | Стадия | Лист | Листов |
|---|---|---|---|
| | РП | 73 | 94 |
| **Развёртки стен. Гардеробная (пом. 3)** М 1:25 | **Кырпан Александр Сергеевич** | | |

выпуск 05.10.2026 · 6add39ab8d · стр. 84 из 137

# Развёртки стен А, Б. Спальня 2 (пом. 4)

Спальня 2 (пом. 4) · вид изнутри помещения · размеры в мм, отметки в м

ПРЕДВАРИТЕЛЬНО · не для производства работ · открыто пунктов: 31 (реестр — л. 6–11)

### Развёртка стены А

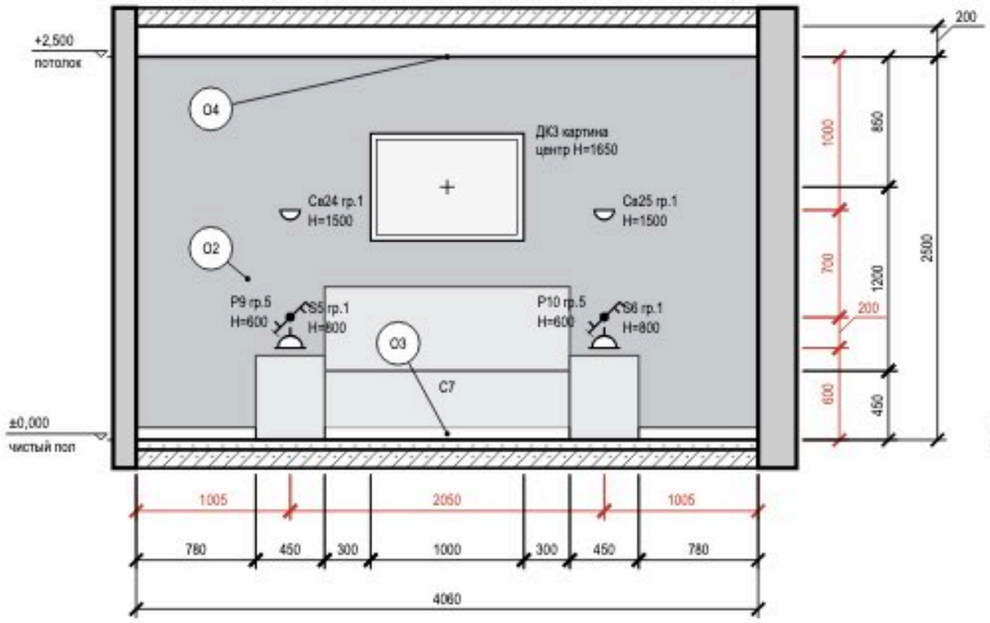


### Развёртка стены Б

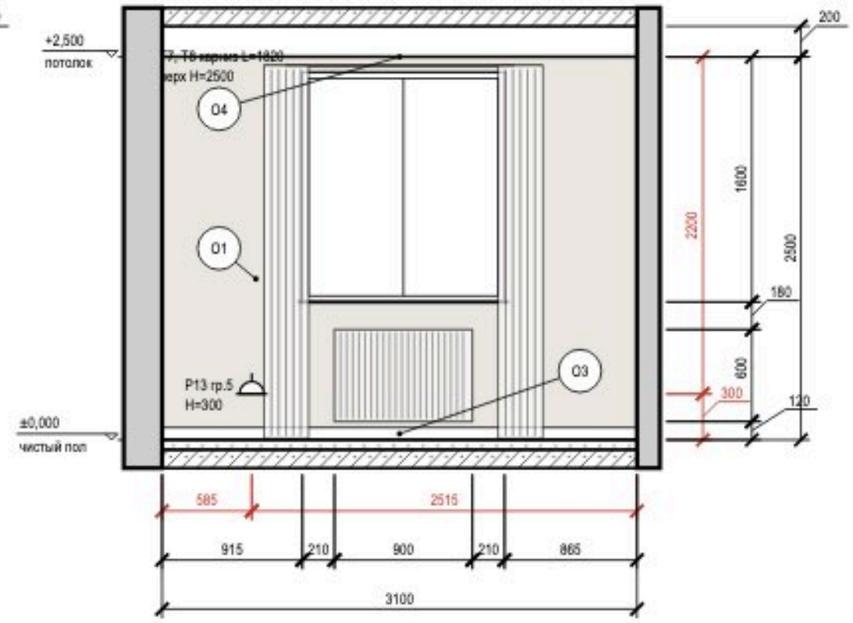


### Схема развёрток (М 1:100)

### Условные обозначения

- розетка с заземляющим контактом; у знака — марка, ×N постов в рамке, гр. — группа щита, Н — высота оси, мм
- выключатель одноклавишный
- выключатель двухклавишный (флажков — по числу клавиш)
- выключатель с проходной или перекрёстной клавишей (обратный флажок); тип клавиши — в подписи
- светильник настенный (бра), Н — высота оси
- привязки точек и выводов от угла и от пола, мм
- мебель и приборы — фасад по расстановке (условно)
- картина (декор): марка Д, крест — центр, Н — высота центра, мм
- карниз (шина) и шторы в собранном виде: марка Т, длина L, верх Н
- окно: проём, рама, подоконник
- радиатор отопления; марка — по плану отопления
- стены и перекрытия в сечении
- окраска: тон — цвет по коду производителя (условно)
- О1 — марка отделки по реестру отделки альбома
- А — марка развёртки: буква стены, стрелка — взгляд

### Ведомость отделки (на листе)

| Марка | Поверхность | Материал, изделие | Цвет, код | Кол. |
|---|---|---|---|---|
| О1 | стены | окраска, Farrow & Ball Modern Emulsion, матовая, подготовка Q3 | Farrow & Ball No. 241 «Skimming Stone» | 5,8 м² |
| О2 | акцентная стена | окраска, Farrow & Ball Modern Emulsion, матовая, подготовка Q3 | Farrow & Ball No. 30 «Hague Blue» | 10,2 м² |
| О3 | плинтус | плинтус МДФ, h 80 мм, аналог: плинтус МДФ под покраску 80×16 | Farrow & Ball No. 241 «Skimming Stone» | 6,3 м |
| О4 | потолок | окраска, Tikkurila Anti-Reflex 2, глубокоматовая, подготовка Q3 | Tikkurila V503 «Winter» | 12,8 м² |

**Допущения и предложения на листе**

Основа листа: размеры сняты со скана плана заказчика по размерным цепочкам, контрольный обмер на объекте не выполнялся (К-13); высота потолка 2700 мм принята: на плане заказчика не указана (К-11); толщины стен приняты: наружные 250 мм, перегородки 150 мм (на плане 85–190 мм) (К-13); разрешённая мощность 15 кВт принята по типовой квартире, технических условий нет (К-14); утолщение стены 190 × 1360 мм и элемент 1470 × 160 мм плана заказчика не определены (К-12); ниши санузла 2 закрыты перегородкой и фальш-стеной: проектное решение, на плане заказчика ниша у входа открыта (К-18); несущие стены не определены: до технического заключения все существующие стены считаются несущими (К-20); окна существующие и сохраняются; подоконная доска и глубина откосов не заданы — приняты, не замерены (К-27).

Знак «*» — принято, не замерено и не подтверждено (замерить на объекте): К-13: отметка существующего пола — отметка существующего пола и верха плинты не замерена: на плане заказчика отметок нет; нивелировка — в задании на обмер (К-13).

См. лист открытых вопросов (лист 6, запись К-11; лист 7, записи К-12–К-14, К-18, К-20; лист 8, запись К-27).

### Примечания

1. Развёртки — вид на стену изнутри помещения, по часовой стрелке; расположение — на схеме листа и на листе 68; размеры — в мм по чистовым поверхностям; отметки — в м от ±0,000; высоты Н — от чистого пола помещения до оси изделия, у декора — до центра.
2. Красные цепочки — привязки электроточек и выводов: по горизонтали от угла чистовых стен, по вертикали от чистого пола, до оси изделия; звенья короче 3 мм на листе вынесены во второй ярус (ближняя к стене цепочка).
3. У знака электроточки: марка (Р — розетка, S — выключатель, Св — светильник, ЭВ — вывод кабеля), ×N — число постов в рамке, гр. — группа щита, Н — высота оси от чистого пола, мм; группы по клавишам выключателя — на листе выключателей.
4. Схема мебели, приборов и декора не является технической документацией для производства мебели; габариты — по паспортам изделий.
5. Картины и зеркала крепить к основанию по паспорту изделия (закладные и анкеры — в перечне скрытых работ); крест — ось центра предмета.
6. Карнизы (шины) — по ведомости текстиля декоратора; длина L и верх Н — по развёртке, крепление — до окраски потолка.
7. Потолок на развёртках — по нижнему уровню У1; другие уровни потолка помещения: У2 +2,600.

1000 мм · печать 1:1

| Изм. | Кол.уч | Лист | № док. | Подп. | Дата |
|---|---|---|---|---|---|
| Разраб. | | Кырпан А.С. | | | 05.10.26 |
| Пров. | | | | | |
| ГИП | | | | | |
| | | | | | |
| Н. контр. | | | | | |
| Утв. | | | | | |

**ГД-2026-003-АИ**

Трёхкомнатная квартира

Общая площадь 78,95* м² · * размеры со скана, не замерены (реестр — п. 6–11, К-13)

Дизайн-проект интерьера трёхкомнатной квартиры

| Стадия | Лист | Листов |
|---|---|---|
| РП | 74 | 94 |

Развёртки стен А, Б. Спальня 2 (пом. 4)

М 1:40

Кырпан Александр Сергеевич

выпуск 05.10.2026 · 6add39ab8d · стр. 85 из 137

# Развёртки стен В, Г. Спальня 2 (пом. 4)

Спальня 2 (пом. 4) · вид изнутри помещения · размеры в мм, отметки в м

ПРЕДВАРИТЕЛЬНО · не для производства работ · открыто пунктов: 31 (реестр — л. 6–11)

### Развёртка стены В

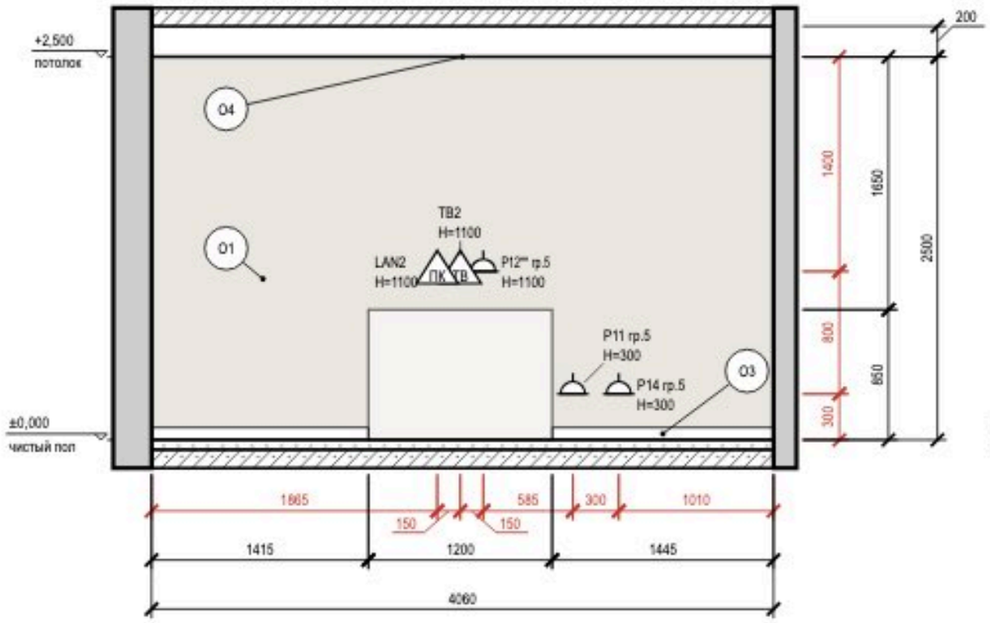


### Развёртка стены Г

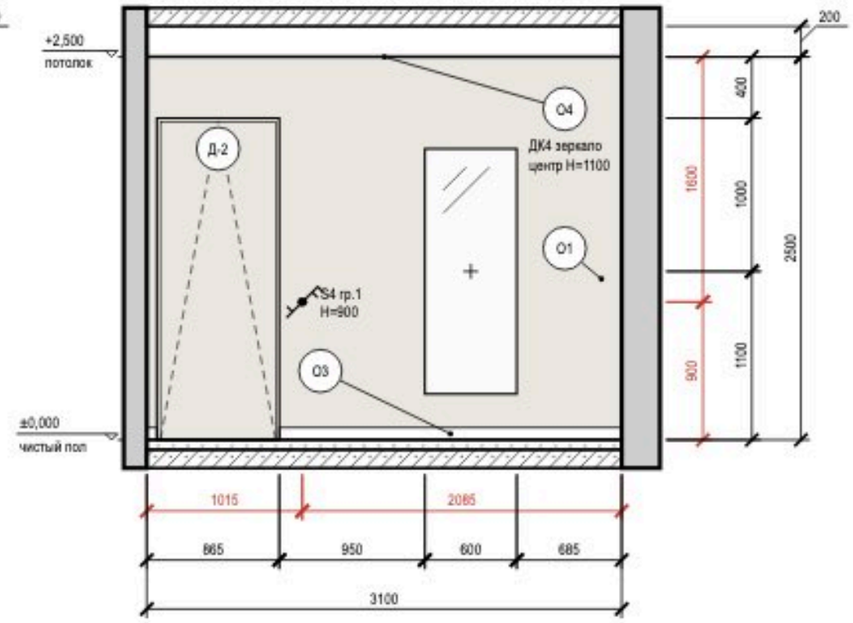


### Схема развёрток (М 1:100)

### Условные обозначения

- розетка с заземляющим контактом; у знака — марка, ×N постов в рамке, гр. — группа щита, H — высота оси, мм
- выключатель одноклавишный
- выключатель двухклавишный (флажков — по числу клавиш)
- выключатель с проходной или перекрёстной клавишей (обратный флажок); тип клавиши — в подписи
- ПК — розетка компьютерная RJ45
- ТВ — розетка телевизионная
- привязки точек и выводов от угла и от пола, мм
- мебель и приборы — фасад по расстановке (условно)
- зеркало: марка Д, крест — центр, H — высота центра, мм
- дверь скрытого монтажа: полотно в плоскости стены (узел — на листе узлов)
- стены и перекрытия в сечении
- окраска: тон — цвет по коду производителя (условно)
- О1 — марка отделки по реестру отделки альбома
- А — марка развёртки: буква стены, стрелка — взгляд

### Ведомость отделки (на листе)

| Марка | Поверхность | Материал, изделие | Цвет, код | Кол. |
|---|---|---|---|---|
| О1 | стены | окраска, Farrow & Ball Modern Emulsion, матовая, подготовка Q3 | Farrow & Ball No. 241 «Skimming Stone» | 16,2 м² |
| О3 | плинтус | плинтус МДФ, h 80 мм, аналог: плинтус МДФ под покраску 80×16 | Farrow & Ball No. 241 «Skimming Stone» | 5,2 м |
| О4 | потолок | окраска, Tikkurila Anti-Reflex 2, глубокоматовая, подготовка Q3 | Tikkurila V503 «Winter» | 12,8 м² |

**Допущения и предложения на листе**

Основа листа: размеры сняты со скана плана заказчика по размерным цепочкам, контрольный обмер на объекте не выполнялся (К-13); высота потолка 2700 мм принята: на плане заказчика не указана (К-11); толщины стен приняты: наружные 250 мм, перегородки 150 мм (на плане 85–190 мм) (К-13); разрешённая мощность 15 кВт принята по типовой квартире, технических условий нет (К-14); утолщение стены 190 × 1360 мм и элемент 1470 × 160 мм плана заказчика не определены (К-12); ниши санузла 2 закрыты перегородкой и фальш-стеной: проектное решение, на плане заказчика ниша у входа открыта (К-18); несущие стены не определены: до технического заключения все существующие стены считаются несущими (К-20); окна существующие и сохраняются; подоконная доска и глубина откосов не заданы — приняты, не замерены (К-27).

Знак «*» — принято, не замерено и не подтверждено (замерить на объекте): К-13: отметка существующего пола — отметка существующего пола и верха плиты не замерена: на плане заказчика отметок нет; нивелировка — в задании на обмер (К-13).

Знак «**» — предложение проектировщика, заказчиком не утверждено (согласовать с заказчиком): К-7: Р12 — высота 1100 мм выше нормы 1 м (ПУЭ 6.6.30) по назначению: питание ТВ над комодом, в одной зоне с выводами ТВ2 и LAN2.

См. лист открытых вопросов (лист 6, записи К-7, К-11; лист 7, записи К-12–К-14, К-18, К-20; лист 8, запись К-27).

### Примечания

1. Развёртки — вид на стену изнутри помещения, по часовой стрелке; расположение — на схеме листа и на листе 68; размеры — в мм по чистовым поверхностям; отметки — в м от ±0,000; высоты H — от чистого пола помещения до оси изделия, у декора — до центра.
2. Красные цепочки — привязки электроточек и выводов: по горизонтали от угла чистовых стен, по вертикали от чистого пола, до оси изделия; звенья короче 3 мм на листе вынесены во второй ярус (ближняя к стене цепочка).
3. У знака электроточки: марка (Р — розетка, S — выключатель, Св — светильник, ЭВ — вывод кабеля), ×N — число постов в рамке, гр. — группа щита, H — высота оси от чистого пола, мм; группы по клавишам выключателя — на листе выключателей.
4. Схема мебели, приборов и декора не является технической документацией для производства мебели; габариты — по паспортам изделий.
5. Картины и зеркала крепить к основанию по паспорту изделия (закладные и анкеры — в перечне скрытых работ); крест — ось центра предмета.
6. Двери скрытого монтажа — полотно в плоскости стены, отделка стены по полотну, плинтус прерывается у короба (узел — на листе узлов).
7. Потолок на развёртках — по нижнему уровню У1; другие уровни потолка помещения: У2 +2,600.

1000 мм · печать 1:1

| Изм. | Кол.уч | Лист | № док. | Подп. | Дата |
|---|---|---|---|---|---|
| Разраб. | | Кырпан А.С. | | | 05.10.26 |
| Пров. | | | | | |
| ГИП | | | | | |
| | | | | | |
| Н. контр. | | | | | |
| Утв. | | | | | |

**ГД-2026-003-АИ**

Трёхкомнатная квартира

Общая площадь 78,95* м² · * размеры со скана, не замерены (реестр — п. 6–11, К-13)

Дизайн-проект интерьера трёхкомнатной квартиры

| Стадия | Лист | Листов |
|---|---|---|
| РП | 75 | 94 |

Развёртки стен В, Г. Спальня 2 (пом. 4)

М 1:40

Кырпан Александр Сергеевич

выпуск 05.10.2026 · 6add39ab8d · стр. 86 из 137

# Развёртки стен А, Б, В. Прихожая (пом. 5)

Прихожая (пом. 5) · вид изнутри помещения · размеры в мм, отметки в м

ПРЕДВАРИТЕЛЬНО · не для производства работ · открыто пунктов: 31 (реестр — л. 6–11)

### Развёртка стены А

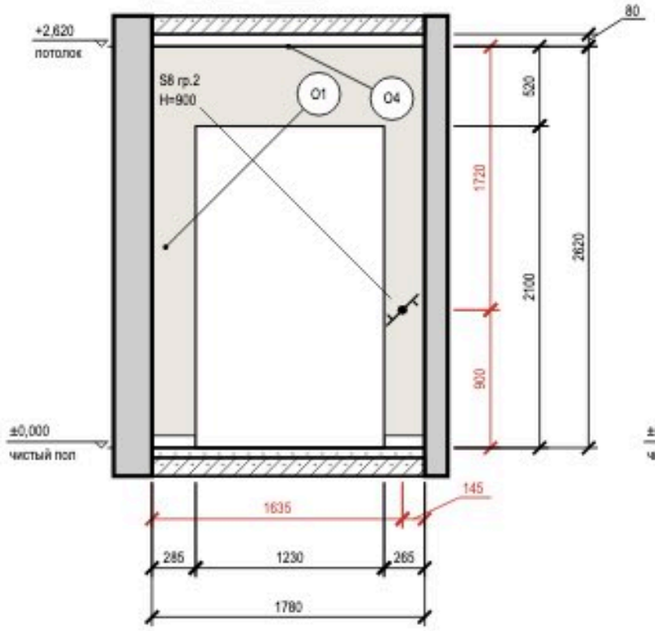


### Развёртка стены Б

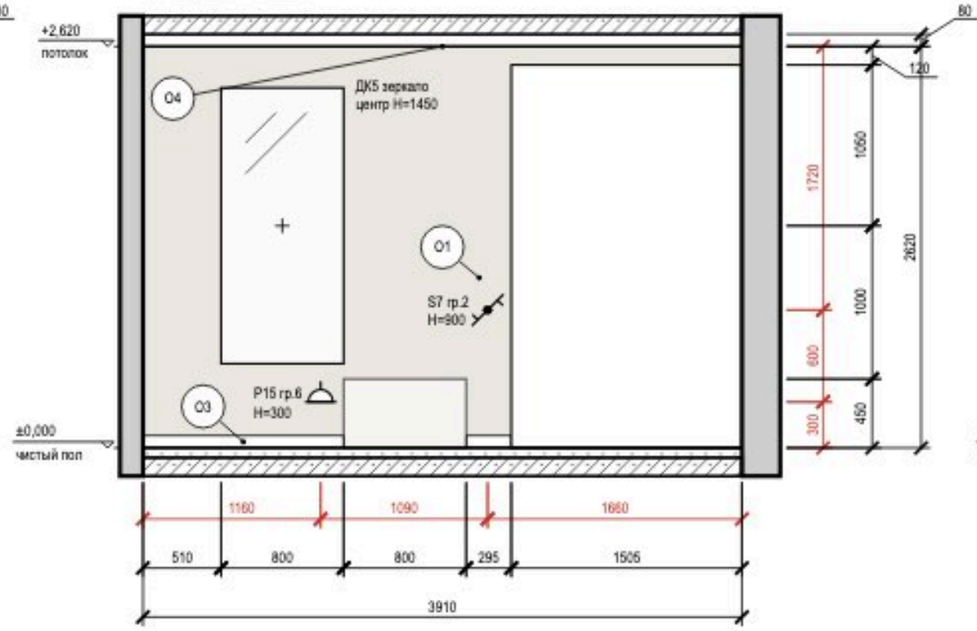


### Развёртка стены В

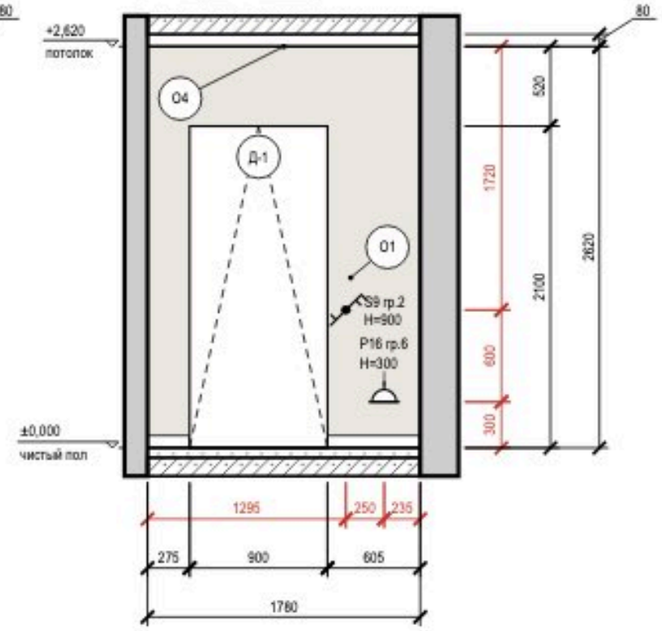


### Схема развёрток (М 1:100)

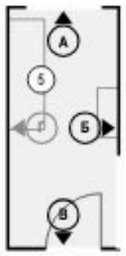


### Условные обозначения

- розетка с заземляющим контактом; у знака — марка, ×N постов в рамке, гр. — группа щита, H — высота оси, мм
- выключатель одноклавишный
- выключатель двухклавишный (флажков — по числу клавиш)
- выключатель с проходной или перекрёстной клавишей (обратный флажок); тип клавиши — в подписи
- привязки точек и выводов от угла и от пола, мм
- мебель и приборы — фасад по расстановке (условно)
- зеркало: марка Д, крест — центр, H — высота центра, мм
- дверной проём; марка двери — в кружке
- стены и перекрытия в сечении
- окраска: тон — цвет по коду производителя (условно)
- О1 — марка отделки по реестру отделки альбома
- А — марка развёртки: буква стены, стрелка — взгляд

### Ведомость отделки (на листе)

| Марка | Поверхность | Материал, изделие | Цвет, код | Кол. |
|---|---|---|---|---|
| О1 | стены | окраска, Farrow & Ball Modern Emulsion, матовая, подготовка Q3 | Farrow & Ball No. 241 «Skimming Stone» | 11,3 м² |
| О3 | плинтус | плинтус МДФ, h 80 мм, аналог: плинтус МДФ под покраску 80×16 | Farrow & Ball No. 241 «Skimming Stone» | 3 м |
| О4 | потолок | окраска, Tikkurila Anti-Reflex 2, глубокоматовая, подготовка Q3 | Tikkurila V503 «Winter» | 7,1 м² |

**Допущения и предложения на листе**

Основа листа: размеры сняты со скана плана заказчика по размерным цепочкам, контрольный обмер на объекте не выполнялся (К-13); высота потолка 2700 мм принята: на плане заказчика не указана (К-11); толщины стен приняты: наружные 250 мм, перегородки 150 мм (на плане 85–190 мм) (К-13); разрешённая мощность 15 кВт принята по типовой квартире, технических условий нет (К-14); утолщение стены 190 × 1360 мм и элемент 1470 × 160 мм плана заказчика не определены (К-12); ниши санузла 2 закрыты перегородкой и фальш-стеной: проектное решение, на плане заказчика ниша у входа открыта (К-18); несущие стены не определены: до технического заключения все существующие стены считаются несущими (К-20); окна существующие и сохраняются; подоконная доска и глубина откосов не заданы — приняты, не замерены (К-27).

Знак «*» — принято, не замерено и не подтверждено (замерить на объекте): К-13: отметка существующего пола — отметка существующего пола и верха плиты не замерена: на плане заказчика отметок нет; нивелировка — в задании на обмер (К-13); К-26: дверь пом. 5 (стена В) — входная дверь существующая; по плану заказчика полотно открывается наружу, в общий коридор — направление взято с плана и на объекте не проверено; остаётся ли существующий блок или он заменяется — не решено (К-26).

См. лист открытых вопросов (лист 6, запись К-11; лист 7, записи К-12–К-14, К-18, К-20; лист 8, записи К-26, К-27).

### Примечания

1. Развёртки — вид на стену изнутри помещения, по часовой стрелке; расположение — на схеме листа и на листе 68; размеры — в мм по чистовым поверхностям; отметки — в м от ±0,000; высоты H — от чистого пола помещения до оси изделия, у декора — до центра.
2. Красные цепочки — привязки электроточек и выводов: по горизонтали от угла чистовых стен, по вертикали от чистого пола, до оси изделия; звенья короче 3 мм на листе вынесены во второй ярус (ближняя к стене цепочка).
3. У знака электроточки: марка (Р — розетка, S — выключатель, Св — светильник, ЭВ — вывод кабеля), ×N — число постов в рамке, гр. — группа щита, H — высота оси от чистого пола, мм; группы по клавишам выключателя — на листе выключателей.
4. Схема мебели, приборов и декора не является технической документацией для производства мебели; габариты — по паспортам изделий.
5. Картины и зеркала крепить к основанию по паспорту изделия (закладные и анкеры — в перечне скрытых работ); крест — ось центра предмета.

1000 мм · печать 1:1

| Изм. | Кол.уч | Лист | № док. | Подп. | Дата |
|---|---|---|---|---|---|
| Разраб. | | Кырпан А.С. | | | 05.10.26 |
| Пров. | | | | | |
| ГИП | | | | | |
| | | | | | |
| Н. контр. | | | | | |
| Утв. | | | | | |

**ГД-2026-003-АИ**

Трёхкомнатная квартира

Общая площадь 78,95* м² · * размеры со скана, не замерены (реестр — п. 6–11, К-13)

Дизайн-проект интерьера трёхкомнатной квартиры

| Стадия | Лист | Листов |
|---|---|---|
| РП | 76 | 94 |

**Развёртки стен А, Б, В. Прихожая (пом. 5)**

М 1:40

Кырпан Александр Сергеевич

выпуск 05.10.2026 · 6add39ab8d · стр. 87 из 137

# Развёртка стены Г. Прихожая (пом. 5)

Прихожая (пом. 5) · вид изнутри помещения · размеры в мм, отметки в м

ПРЕДВАРИТЕЛЬНО · не для производства работ · открыто пунктов: 31 (реестр — л. 6–11)

## Развёртка стены Г

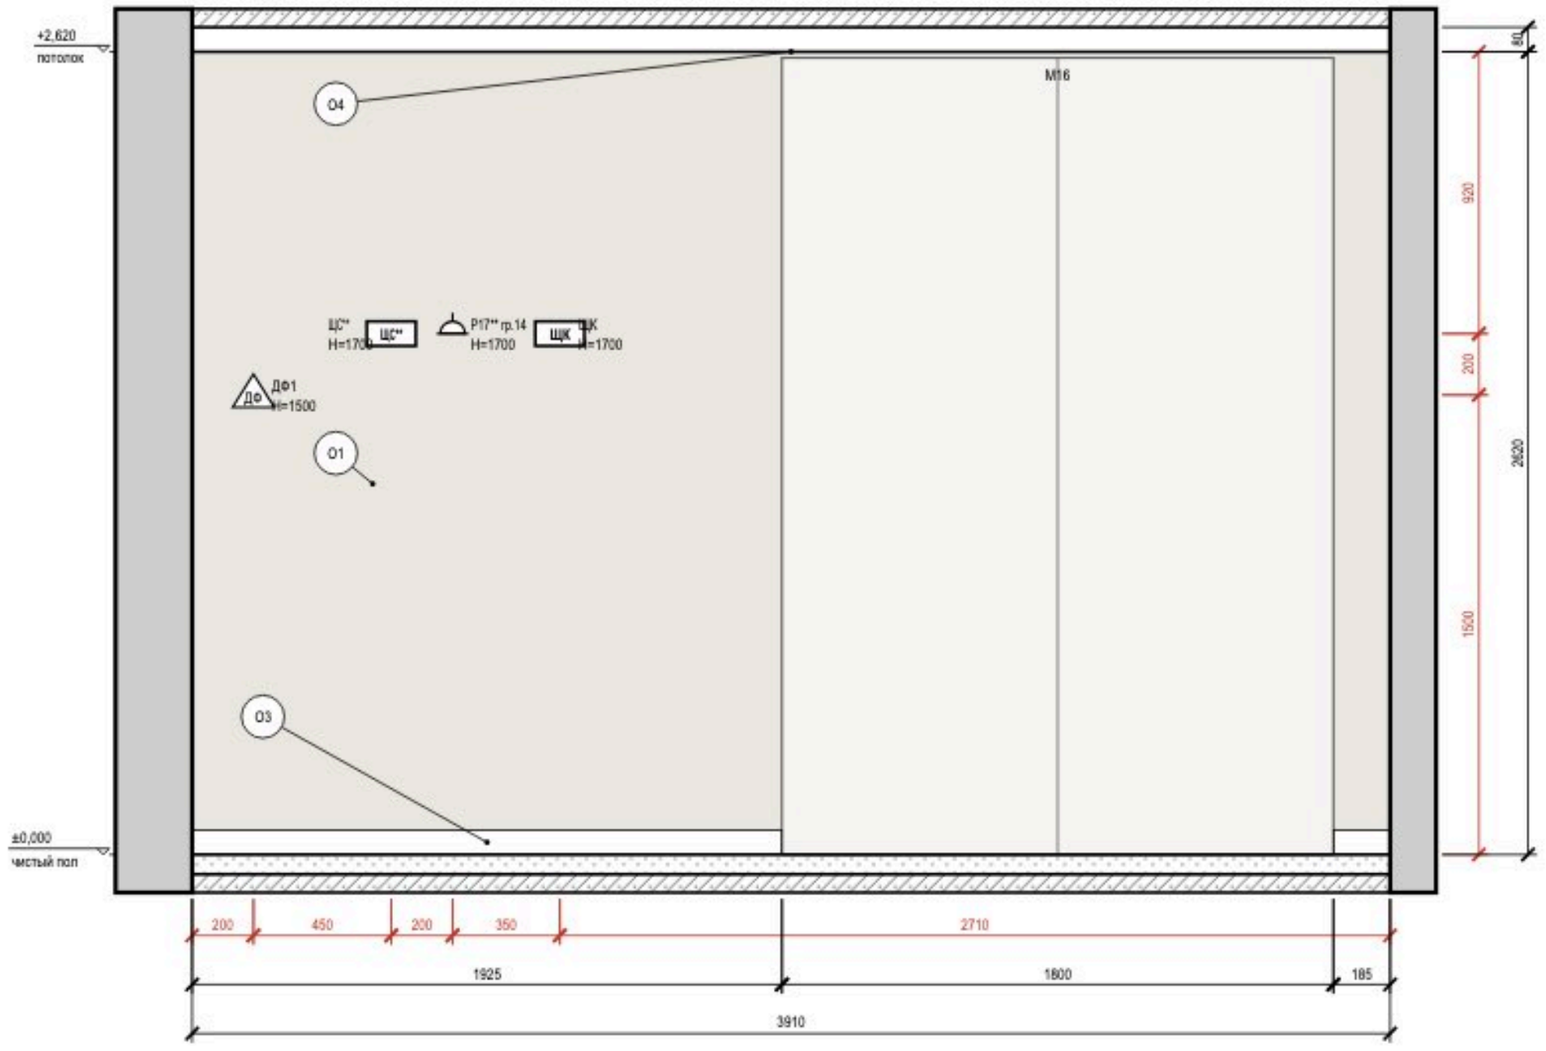


Допущения и предложения на листе. Основа листа: размеры сняты со скана плана заказчика по размерным цепочкам, контрольный обмер на объекте не выполнялся (К-13); высота потолка 2700 мм принята: на плане заказчика не указана (К-11); толщины стен приняты: наружные 250 мм, перегородки 150 мм (на плане 85–190 мм) (К-13); разрешённая мощность 15 кВт принята по типовой квартире, технических условий нет (К-14); утопление стены 190 × 1360 мм и элемент 1470 × 160 мм плана заказчика не определены (К-12); ниши санузла 2 закрыты перегородкой и фальш-стеной: проектное решение, на плане заказчика ниша у входа открыта (К-18); несущие стены не определены: до технического заключения все существующие стены считаются несущими (К-20); окна существующие и сохраняются; подоконная доска и глубина откосов не заданы — приняты, не замерены (К-27). Знак «*» — принято, не замерено и не подтверждено (замерить на объекте): К-13: отметка существующего пола — отметка существующего пола и верха плиты не замерена: на плане заказчика отметок нет; нивелировка — в задании на обмер (К-13); К-26: дверь пом. 5 (стена В) — входная дверь существующая; по плану заказчика полотно открывается наружу, в общий коридор — направление взято с плана и на объекте не проверено; остаётся ли существующий блок или он заменяется — не решено (К-26). Знак «**» — предложение проектировщика, заказчиком не утверждено (согласовать с заказчиком): ИЗ-17: ЩС — щит слаботочный: место и состав; К-7: Р17 — высота 1700 мм выше нормы 1 м (ПУЭ 6.6.30) по назначению: питание слаботочного щита ЩС, рядом со щитом на его высоте. См. лист открытых вопросов (лист 6, записи К-7, К-11; лист 7, записи К-12–К-14, К-18, К-20; лист 8, записи К-26, К-27; лист 11, запись ИЗ-17).

## Примечания

1. Развёртки — вид на стену изнутри помещения, по часовой стрелке; расположение — на схеме листа и на листе 68; размеры — в мм по чистовым поверхностям; отметки — в м от ±0,000; высоты Н — от чистого пола помещения до оси изделия, у декора — до центра.
2. Красные цепочки — привязки электроточек и выводов: по горизонталям от угла чистовых стен, по вертикали от чистого пола, до оси изделия; звенья короче 3 мм на листе вынесены во второй ярус (ближние к стене цепочка).
3. У знака электроточки: марка (Р — розетка, S — выключатель, Св — светильник, ЭВ — вывод кабеля), ×N — число постов в рамке, гр. — группа щита, Н — высота оси от чистого пола, мм; группы по клавишам выключателя — на листе выключателей.
4. Схема мебели, приборов и декора не является технической документацией для производства мебели; габариты — по паспортам изделий.

1000 мм · печать 1:1

## Схема развёрток (М 1:100)

## Условные обозначения

- розетка с заземляющим контактом; у знака — марка, ×N постов в рамке, гр. — группа щита, Н — высота оси, мм
- Дф — трубка или монитор домофона
- ЩК — щит квартирный
- привязки точек и выводов от угла и от пола, мм
- мебель и приборы — фасад по расстановке (условно)
- стены и перекрытия в сечении
- окраска: тон — цвет по коду производителя (условно)
- О1 — марка отделки по реестру отделки альбома
- А — марка развёртки: буква стены, стрелка — взгляд

## Ведомость отделки (на листе)

| Марка | Поверхность | Материал, изделие | Цвет, код | Кол. |
|---|---|---|---|---|
| О1 | стены | окраска, Farrow & Ball Modern Emulsion, матовая, подготовка Q3 | Farrow & Ball No. 241 «Skimming Stone» | 10,2 м² |
| О3 | плинтус | плинтус МДФ, h 80 мм, аналог: плинтус МДФ под покраску 80×16 | Farrow & Ball No. 241 «Skimming Stone» | 2,1 м |
| О4 | потолок | окраска, Tikkurila Anti-Reflex 2, глубокоматовая, подготовка Q3 | Tikkurila V503 «Winter» | 7,1 м² |

| Изм. | Кол.уч | Лист | № док. | Подп. | Дата |
|---|---|---|---|---|---|
| Разраб. | | Кырлан А.С. | | | 05.10.26 |
| Пров. | | | | | |
| ГИП | | | | | |
| Н. контр. | | | | | |
| Утв. | | | | | |

**ГД-2026-003-АИ**

Трёхкомнатная квартира

Общая площадь 78,95* м² · * размеры со скана, не замерены (реестр — л. 6–11, К-13)

Дизайн-проект интерьера трёхкомнатной квартиры

| Стадия | Лист | Листов |
|---|---|---|
| РП | 77 | 94 |

**Развёртка стены Г. Прихожая (пом. 5)**

М 1:20

**Кырлан Александр Сергеевич**

выпуск 05.10.2026 № 6add3ab8d · стр. 88 из 137

# Развёртка стены Б2. Кухня-гостиная (пом. 6), кухонный фронт

Кухня-гостиная (пом. 6) · вид изнутри помещения · размеры в мм, отметки в м

ПРЕДВАРИТЕЛЬНО · не для производства работ · открыто пунктов: 31 (реестр — л. 6–11)

## Развёртка стены Б2

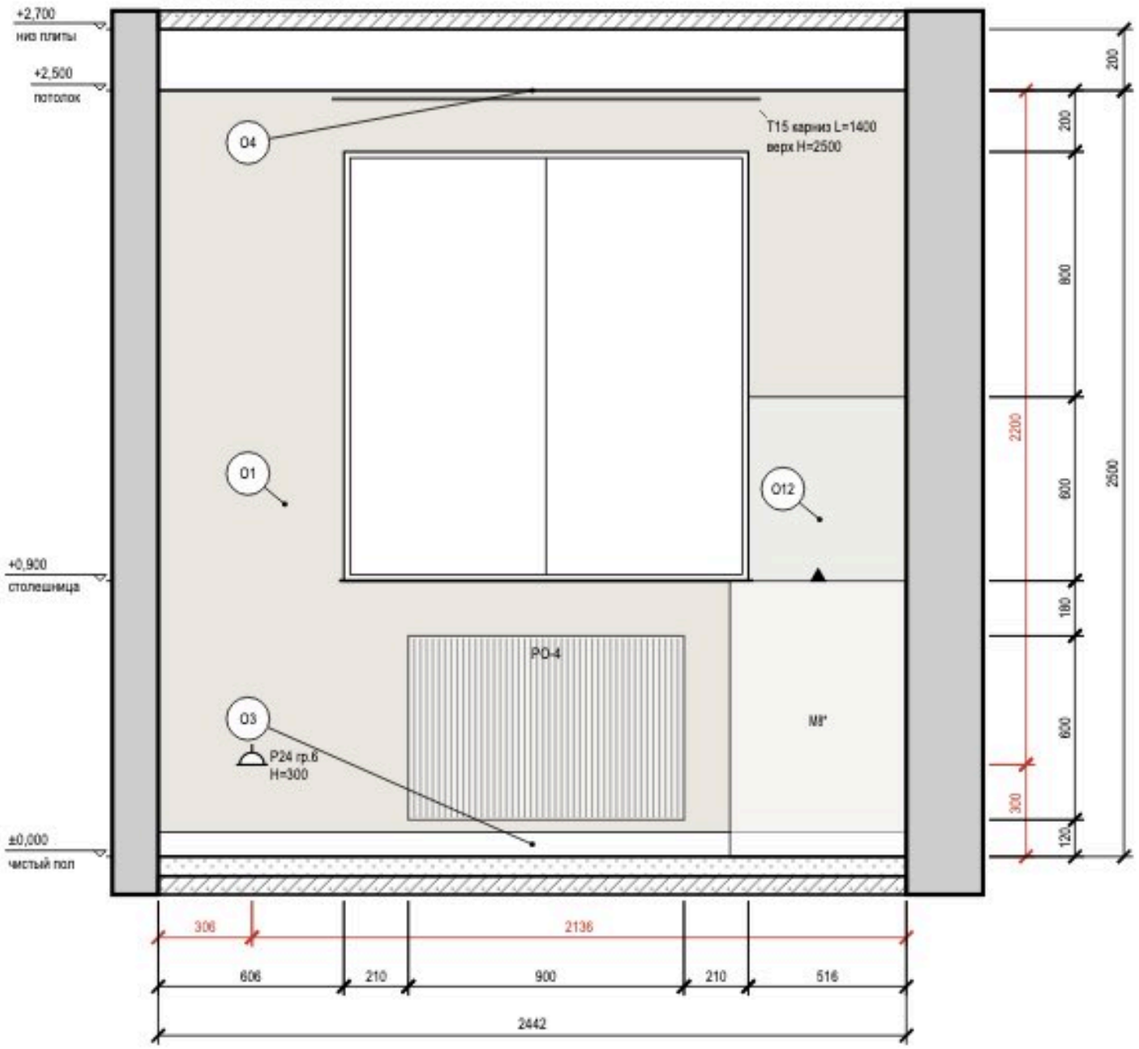


## Схема развёрток (М 1:100)

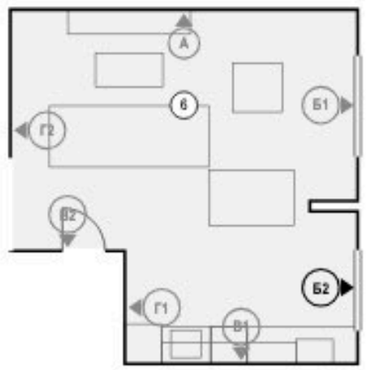


## Условные обозначения

- розетка с заземляющим контактом; у знака — марка, ×N постов в рамке, гр. — группа щита, H — высота оси, мм
- привязки точек и выводов от угла и от пола, мм
- мебель и приборы — фасад по расстановке (условно)
- карниз (шина) и шторы в собранном виде: марка Т, длина L, верх H
- окно: проём, рама, подоконник
- радиатор отопления; марка — по плану отопления
- стены и перекрытия в сечении
- плитка: сетка швов по формату, ▲ — ось старта
- окраска: тон — цвет по коду производителя (условно)
- О1 — марка отделки по реестру отделки альбома
- А — марка развёртки: буква стены, стрелка — взгляд

## Ведомость отделки (на листе)

| Марка | Поверхность | Материал, изделие | Цвет, код | Кол. |
|---|---|---|---|---|
| О1 | стены | окраска, Farrow & Ball Modern Emulsion, матовая, подготовка Q3 | Farrow & Ball No. 241 «Skimming Stone» | 3,9 м² |
| О3 | плинтус | плинтус МДФ, h 80 мм, аналог: плинтус МДФ под покраску 80×16 | Farrow & Ball No. 241 «Skimming Stone» | 2,4 м |
| О4 | потолок | окраска, Tikkurila Anti-Reflex 2, глубокоматовая, подготовка Q3 | Tikkurila V503 «Winter» | 29,2 м² |
| О12 | фартук | керамогранит, 1200×600×9 мм, аналог: керамогранит под травертин, матовый, затирка CG2WA | | 0,3 м² |

**Допущения и предложения на листе**

Основа листа: размеры сняты со скана плана заказчика по размерным цепочкам, контрольный обмер на объекте не выполнялся (К-13); высота потолка 2700 мм принята: на плане заказчика не указана (К-11); толщины стен приняты: наружные 250 мм, перегородки 150 мм (на плане 85–190 мм) (К-13); разрешённая мощность 15 кВт принята по типовой квартире, технических условий нет (К-14); утолщение стены 190 × 1360 мм и элемент 1470 × 160 мм плана заказчика не определены (К-12); ниши санузла 2 закрыты перегородкой и фальш-стеной: проектное решение, на плане заказчика ниша у входа открыта (К-18); несущие стены не определены: до технического заключения все существующие стены считаются несущими (К-20); окна существующие и сохраняются; подоконная доска и глубина откосов не заданы — приняты, не замерены (К-27).

Знак «*» — принято, не замерено и не подтверждено (замерить на объекте): К-8: М8; К-13: отметка существующего пола — отметка существующего пола и верха плиты не замерена: на плане заказчика отметок нет; нивелировка — в задании на обмер (К-13).

См. лист открытых вопросов (лист 6, записи К-8, К-11; лист 7, записи К-12–К-14, К-18, К-20; лист 8, запись К-27).

## Примечания

1. Развёртки — вид на стену изнутри помещения, по часовой стрелке; расположение — на схеме листа и на листе 68; размеры — в мм по чистовым поверхностям; отметки — в м от ±0,000; высоты H — от чистого пола помещения до оси изделия, у декора — до центра.
2. Красные цепочки — привязки электроточек и выводов: по горизонтали от угла чистовых стен, по вертикали от чистого пола, до оси изделия; звенья короче 3 мм на листе вынесены во второй ярус (ближние к стене цепочка).
3. У знака электроточки: марка (Р — розетка, S — выключатель, Св — светильник, ЭВ — вывод кабеля), ×N — число постов в рамке, гр. — группа щита, H — высота оси от чистого пола, мм; группы по клавишам выключателя — на листе выключателей.
4. Схема мебели, приборов и декора не является технической документацией для производства мебели; габариты — по паспортам изделий.
5. Карнизы (шины) — по ведомости текстиля декоратора; длина L и верх H — по развёртке, крепление — до окраски потолка.
6. Высота фартука принята 600 мм над столешницей там, где нет навесных модулей и высота фартука не задана.
7. Выводы кухонной техники — по утверждённому проекту кухни: привязки выводов даются от осей модулей гарнитура.
8. Потолок на развёртках — по нижнему уровню У1; другие уровни потолка помещения: У2 +2,600.

1000 мм · печать 1:1

| Изм. | Кол.уч | Лист | № док. | Подп. | Дата |
|---|---|---|---|---|---|
| Разраб. | | Кырпан А.С. | | | 05.10.26 |
| Пров. | | | | | |
| ГИП | | | | | |
| | | | | | |
| Н. контр. | | | | | |
| Утв. | | | | | |

**ГД-2026-003-АИ**

Трёхкомнатная квартира

Общая площадь 78,95* м² · * размеры со скана, не замерены (реестр — п. 6–11, К-13)

Дизайн-проект интерьера трёхкомнатной квартиры

| Стадия | Лист | Листов |
|---|---|---|
| РП | 78 | 94 |

**Развёртка стены Б2. Кухня-гостиная (пом. 6), кухонный фронт**

М 1:20

**Кырпан Александр Сергеевич**

выпуск 05.10.2026 · 6add39ab8d · стр. 89 из 137

# Развёртка стены В1. Кухня-гостиная (пом. 6), кухонный фронт

Кухня-гостиная (пом. 6) · вид изнутри помещения · размеры в мм, отметки в м

ПРЕДВАРИТЕЛЬНО · не для производства работ · открыто пунктов: 31 (реестр — л. 6–11)

## Развёртка стены В1

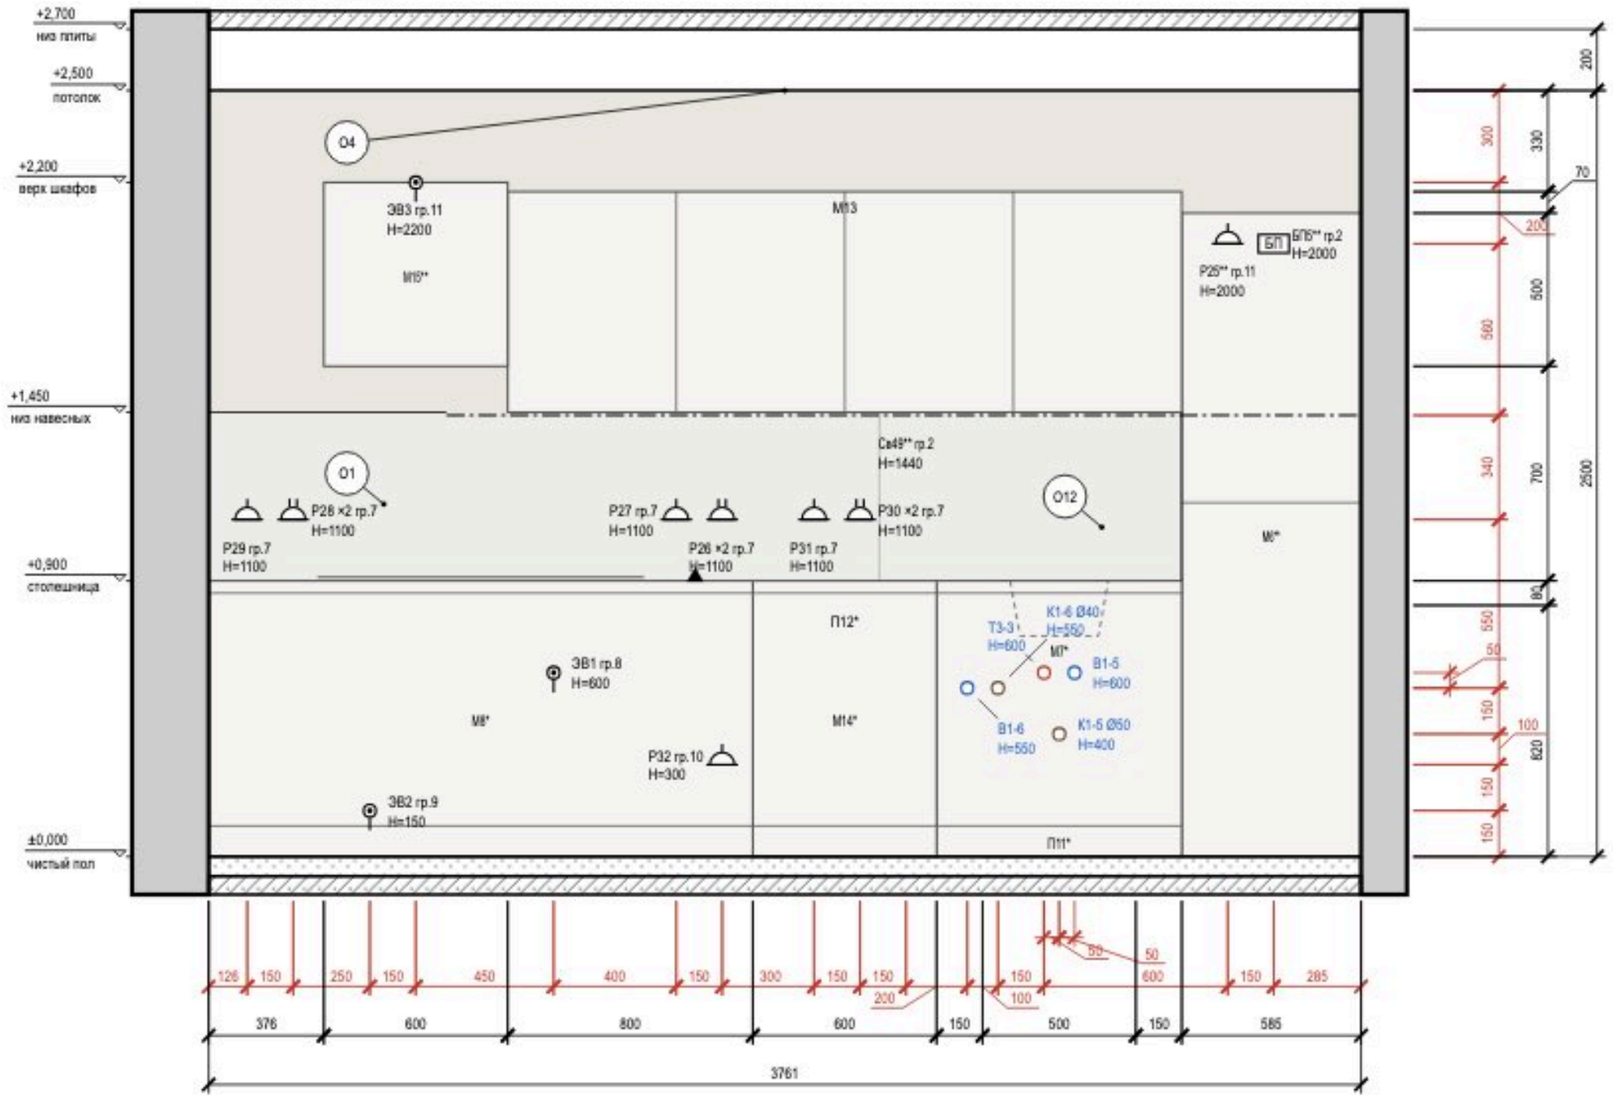


### Схема развёрток (М 1:100)

### Условные обозначения

- розетка с заземляющим контактом; у знака — марка, ×N постов в рамке, гр. — группа щита, Н — высота оси, мм
- вывод кабеля для подключения прибора (без розетки), марка ЭВ
- светодиодная лента в профиле / в карнизе короба
- БП — блок питания LED, с доступом (люк от 100×100 мм)
- вывод В1 (код — в ведомости привязок)
- вывод Т3 (код — в ведомости привязок)
- вывод К1 (код — в ведомости привязок)
- привязки точек и выводов от угла и от пола, мм
- мебель и приборы — фасад по расстановке (условно)
- стены и перекрытия в сечении
- плитка: сетка швов по формату, ▲ — ось старта
- окраска: тон — цвет по коду производителя (условно)
- О1 — марка отделки по реестру отделки альбома
- А — марка развёртки: буква стены, стрелка — взгляд

Допущения и предложения на листе. Основа листа: размеры сняты со скана плана заказчика по размерным цепочкам, контрольный обмер на объекте не выполнялся (К-13); высота потолка 2700 мм принята: на плане заказчика не указана (К-11); толщины стен приняты: наружные 250 мм, перегородки 150 мм (на плане 85–190 мм) (К-13); разрешённая мощность 15 кВт принята по типовой квартире, технических условий нет (К-14); утолщение стены 190 × 1360 мм и элемент 1470 × 160 мм плана заказчика не определены (К-12); ниши санузла 2 закрыты перегородкой и фальш-стенкой: проектное решение, на плане заказчика ниша у входа открыта (К-18); несущие стены не определены: до технического заключения все существующие стены считаются несущими (К-20); окна существующие и сохраняются; подоконная доска и глубина откосов не заданы — приняты, не замерены (К-27). Знак «*» — принято, не замерено (замерить): К-13: отметка существующего пола. Знак «**» — предложено, не утверждено (согласовать): ИЗ-3: Св49, БП5; К-7, К-8: Р25. См. лист открытых вопросов (лист 6, записи К-7, К-8, К-11; лист 7, записи К-12–К-14, К-18, К-20; лист 8, запись К-27; лист 9, записи ИЗ-3, ИЗ-5).

## Примечания

1. Развёртки — вид на стену изнутри помещения, по часовой стрелке; расположение — на схеме листа и на листе 68; размеры — в мм по чистовым поверхностям; отметки — в м от ±0,000; высоты Н — от чистого пола помещения до оси изделия, у декора — до центра.
2. Красные цепочки — привязки электроточек и выводов: по горизонтали от угла чистовых стен, по вертикали от чистого пола, до оси изделия; звенья короче 3 мм на листе вынесены во второй ярус (ближняя к стене цепочка).
3. У знака электроточки: марка (Р — розетка, S — выключатель, Св — светильник, ЭВ — вывод кабеля), ×N — число постов в рамке, гр. — группа щита, Н — высота оси от чистого пола, мм; группы по клавишам выключателя — на листе выключателей.
4. Схема мебели, приборов и декора не является технической документацией для производства мебели; габариты — по паспортам изделий (* — высота не задана в проекте, показана по типовому изделию).
5. Выводы кухонной техники — по утверждённому проекту кухни: привязки выводов даются от осей модулей гарнитура.
6. Потолок на развёртках — по нижнему уровню У1; другие уровни потолка помещения: У2 +2,600.

1000 мм · печать 1:1

| Изм. | Кол.уч | Лист | № док. | Подп. | Дата |
|---|---|---|---|---|---|
| Разраб. | | Кырпан А.С. | | | 05.10.26 |
| Пров. | | | | | |
| ГИП | | | | | |
| Н. контр. | | | | | |
| Утв. | | | | | |

**ГД-2026-003-АИ**

Трёхкомнатная квартира

Общая площадь 78,95* м² · * размеры со скана, не замерены (реестр — п. 6–11, К-13)

Дизайн-проект интерьера трёхкомнатной квартиры

| Стадия | Лист | Листов |
|---|---|---|
| РП | 79 | 94 |

**Развёртка стены В1. Кухня-гостиная (пом. 6), кухонный фронт**

М 1:20

**Кырпан Александр Сергеевич**

выпуск 05.10.2026 № 6add39ab8d · стр. 90 из 137

# Развёртки стен А, Б1. Кухня-гостиная (пом. 6)

Кухня-гостиная (пом. 6) · вид изнутри помещения · размеры в мм, отметки в м

ПРЕДВАРИТЕЛЬНО · не для производства работ · открыто пунктов: 31 (реестр — л. 6–11)

### Развёртка стены А

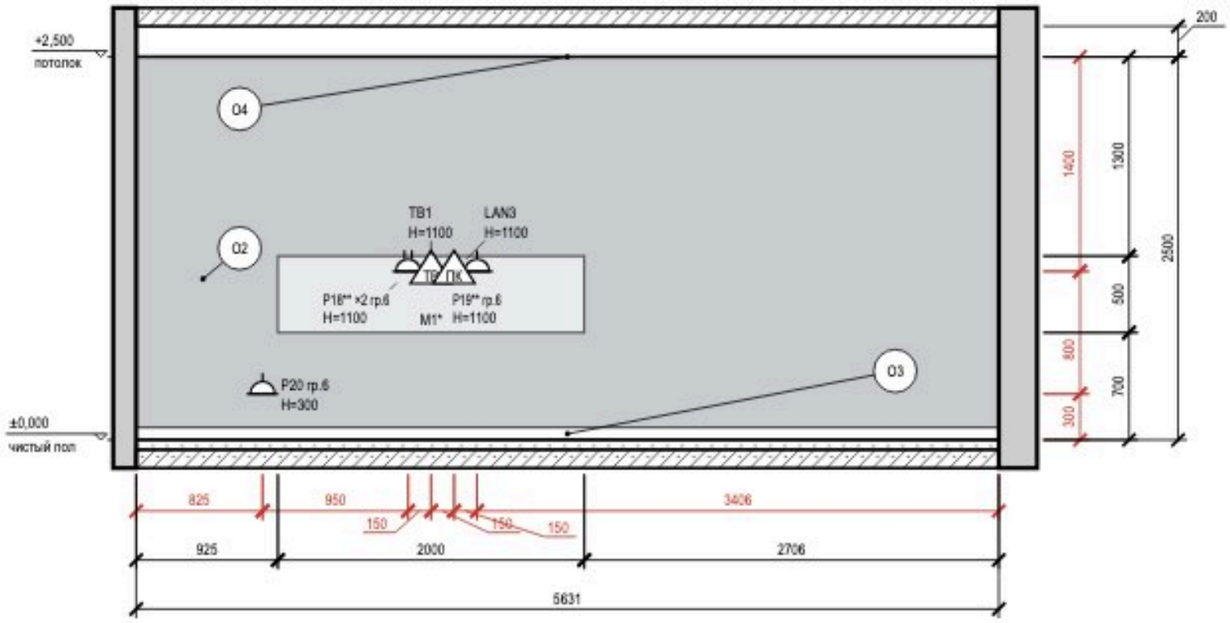


### Развёртка стены Б1

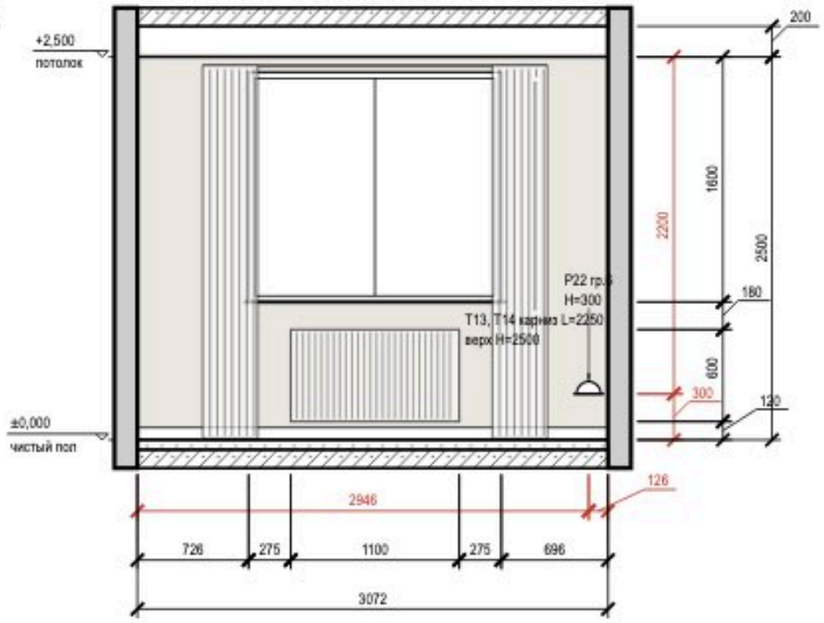


### Схема развёрток (М 1:100)

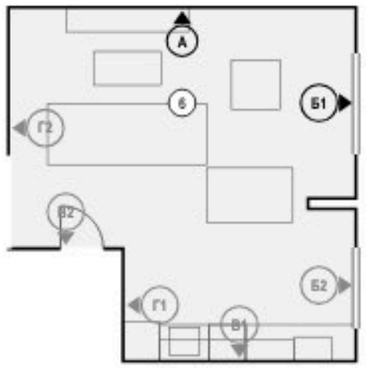


### Условные обозначения

- розетка с заземляющим контактом; у знака — марка, ×N постов в рамке, гр. — группа щита, H — высота оси, мм
- розетка компьютерная RJ45
- розетка телевизионная
- привязки точек и выводов от угла и от пола, мм
- мебель и приборы — фасад по расстановке (условно)
- карниз (шина) и шторы в собранном виде: марка T, длина L, верх H
- окно: проём, рама, подоконник
- радиатор отопления; марка — по плану отопления
- стены и перекрытия в сечении
- окраска: тон — цвет по коду производителя (условно)
- О1 — марка отделки по реестру отделки альбома
- А — марка развёртки: буква стены, стрелка — взгляд

### Ведомость отделки (на листе)

| Марка | Поверхность | Материал, изделие | Цвет, код | Кол. |
|---|---|---|---|---|
| О1 | стены | окраска, Farrow & Ball Modern Emulsion, матовая, подготовка Q3 | Farrow & Ball No. 241 «Skimming Stone» | 5,2 м² |
| О2 | акцентная стена | окраска, Farrow & Ball Modern Emulsion, матовая, подготовка Q3 | Farrow & Ball No. 30 «Hague Blue» | 14,1 м² |
| О3 | плинтус | плинтус МДФ, h 80 мм, аналог: плинтус МДФ под покраску 80×16 | Farrow & Ball No. 241 «Skimming Stone» | 8,7 м |
| О4 | потолок | окраска, Tikkurila Anti-Reflex 2, глубокоматовая, подготовка Q3 | Tikkurila V503 «Winter» | 29,2 м² |

**Допущения и предложения на листе**

Основа листа: размеры сняты со скана плана заказчика по размерным цепочкам, контрольный обмер на объекте не выполнялся (К-13); высота потолка 2700 мм принята: на плане заказчика не указана (К-11); толщины стен приняты: наружные 250 мм, перегородки 150 мм (на плане 85–190 мм) (К-13); разрешённая мощность 15 кВт принята по типовой квартире, технических условий нет (К-14); утолщение стены 190 × 1360 мм и элемент 1470 × 160 мм плана заказчика не определены (К-12); ниши санузла 2 закрыты перегородкой и фальш-стеной: проектное решение, на плане заказчика ниша у входа открыта (К-18); несущие стены не определены: до технического заключения все существующие стены считаются несущими (К-20); окна существующие и сохраняются; подоконная доска и глубина откосов не заданы — приняты, не замерены (К-27).

Знак «*» — принято, не замерено и не подтверждено (замерить на объекте): К-13: отметка существующего пола — отметка существующего пола и верха плиты не замерена: на плане заказчика отметок нет; нивелировка — в задании на обмер (К-13).

Знак «**» — предложение проектировщика, заказчиком не утверждено (согласовать с заказчиком): К-7: Р18 — высота 1100 мм выше нормы 1 м (ПУЭ 6.6.30) по назначению: питание ТВ, в одной зоне с выводами ТВ1 и LAN3; Р19 — высота 1100 мм выше нормы 1 м (ПУЭ 6.6.30) по назначению: питание приставки ТВ, в одной зоне с выводами ТВ1 и LAN3.

См. лист открытых вопросов (лист 6, записи К-7, К-11; лист 7, записи К-12–К-14, К-18, К-20; лист 8, запись К-27).

### Примечания

1. Развёртки — вид на стену изнутри помещения, по часовой стрелке; расположение — на схеме листа и на листе 68; размеры — в мм по чистовым поверхностям; отметки — в м от ±0,000; высоты H — от чистого пола помещения до оси изделия, у декора — до центра.
2. Красные цепочки — привязки электроточек и выводов: по горизонтали от угла чистовых стен, по вертикали от чистого пола, до оси изделия; звенья короче 3 мм на листе вынесены во второй ярус (ближняя к стене цепочка).
3. У знака электроточки: марка (Р — розетка, S — выключатель, Св — светильник, ЭВ — вывод кабеля), ×N — число постов в рамке, гр. — группа щита, H — высота оси от чистого пола, мм; группы по клавишам выключателя — на листе выключателей.
4. Схема мебели, приборов и декора не является технической документацией для производства мебели; габариты — по паспортам изделий (* — высота не задана в проекте, показана по типовому изделию).
5. Карнизы (шины) — по ведомости текстиля декоратора; длина L и верх H — по развёртке, крепление — до окраски потолка.
6. Потолок на развёртках — по нижнему уровню У1; другие уровни потолка помещения: У2 +2,600.
7. Линии узора (швы плитки, складки штор, рёбра радиаторов) прерываются у знаков и выносок — просвет между линиями не менее 0,7 мм.

1000 мм · печать 1:1

| | | | | | | | |
|---|---|---|---|---|---|---|---|
| | | | | | | ГД-2026-003-АИ | |
| | | | | | | Трёхкомнатная квартира | |
| | | | | | | Общая площадь 78,95* м² · * размеры со скана, не замерены (реестр — п. 6–11, К-13) | |
| Изм. | Кол.уч | Лист | № док. | Подп. | Дата | Дизайн-проект интерьера трёхкомнатной квартиры | Стадия: РП; Лист: 80; Листов: 94 |
| Разраб. | | Кырпан А.С. | | | 05.10.26 | | |
| Пров. | | | | | | | |
| ГИП | | | | | | | |
| Н. контр. | | | | | | Развёртки стен А, Б1. Кухня-гостиная (пом. 6) М 1:40 | Кырпан Александр Сергеевич |
| Утв. | | | | | | | |

выпуск 05.10.2026 ⚲ 6add39ab8d · стр. 91 из 137

# Развёртки стен В2, Г1, Г2. Кухня-гостиная (пом. 6)

Кухня-гостиная (пом. 6) · вид изнутри помещения · размеры в мм, отметки в м

ПРЕДВАРИТЕЛЬНО · не для производства работ · открыто пунктов: 31 (реестр — л. 6–11)

**Развёртка стены В2**

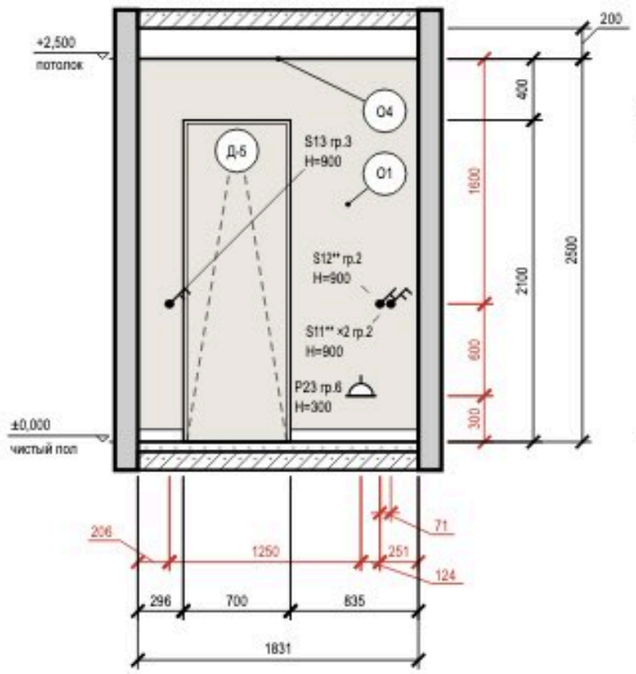


**Развёртка стены Г1**

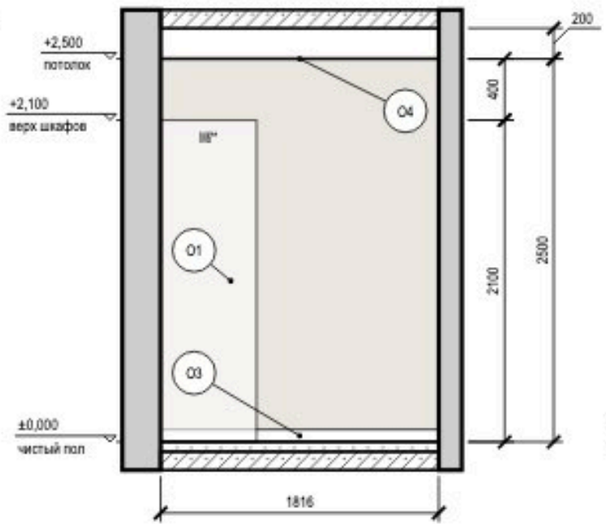


**Развёртка стены Г2**

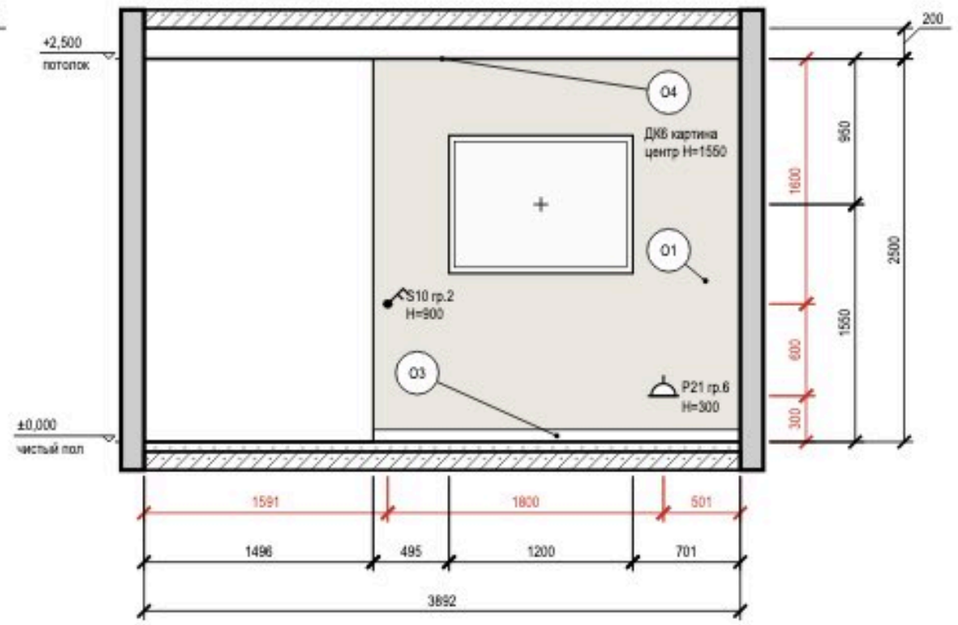


## Схема развёрток (М 1:100)

## Условные обозначения

- розетка с заземляющим контактом; у знака — марка, ×N постов в рамке, гр. — группа щита, Н — высота оси, мм
- выключатель одноклавишный
- выключатель двухклавишный (флажков — по числу клавиш)
- привязки точек и выводов от угла и от пола, мм
- мебель и приборы — фасад по расстановке (условно)
- картина (декор): марка Д, крест — центр, Н — высота центра, мм
- дверь скрытого монтажа: полотно в плоскости стены (узел — на листе узлов)
- дверной проём; марка двери — в кружке
- стены и перекрытия в сечении
- окраска: тон — цвет по коду производителя (условно)
- О1 — марка отделки по реестру отделки альбома
- А — марка развёртки: буква стены, стрелка — взгляд

## Ведомость отделки (на листе)

| Марка | Поверхность | Материал, изделие | Цвет, код | Кол. |
|---|---|---|---|---|
| О1 | стены | окраска, Farrow & Ball Modern Emulsion, матовая, подготовка Q3 | Farrow & Ball No. 241 «Skimming Stone» | 13,6 м² |
| О3 | плинтус | плинтус МДФ, h 80 мм, аналог: плинтус МДФ под покраску 80×16 | Farrow & Ball No. 241 «Skimming Stone» | 5,3 м |
| О4 | потолок | окраска, Tikkurila Anti-Reflex 2, глубокоматовая, подготовка Q3 | Tikkurila V503 «Winter» | 29,2 м² |

**Допущения и предложения на листе**

Основа листа: размеры сняты со скана плана заказчика по размерным цепочкам, контрольный обмер на объекте не выполнялся (К-13); высота потолка 2700 мм принята: на плане заказчика не указана (К-11); толщины стен приняты: наружные 250 мм, перегородки 150 мм (на плане 85–190 мм) (К-13); разрешённая мощность 15 кВт принята по типовой квартире, технических условий нет (К-14); утолщение стены 190 × 1360 мм и элемент 1470 × 160 мм плана заказчика не определены (К-12); ниши санузла 2 закрыты перегородкой и фальш-стеной: проектное решение, на плане заказчика ниша у входа открыта (К-18); несущие стены не определены: до технического заключения все существующие стены считаются несущими (К-20); окна существующие и сохраняются; подоконная доска и глубина откосов не заданы — приняты, не замерены (К-27).

Знак «*» — принято, не замерено и не подтверждено (замерить на объекте): К-13: отметка существующего пола — отметка существующего пола и верха плиты не замерена: на плане заказчика отметок нет; нивелировка — в задании на обмер (К-13).

Знак «**» — предложение проектировщика, заказчиком не утверждено (согласовать с заказчиком): ИЗ-3: S11, S12 — светорегулятор добавлен разработчиком проекта; ИЗ-5, К-8: М6.

См. лист открытых вопросов (лист 6, записи К-8, К-11; лист 7, записи К-12–К-14, К-18, К-20; лист 8, запись К-27; лист 9, записи ИЗ-3, ИЗ-5).

## Примечания

1. Развёртки — вид на стену изнутри помещения, по часовой стрелке; расположение — на схеме листа и на листе 68; размеры — в мм по чистовым поверхностям; отметки — в м от ±0,000; высоты Н — от чистого пола помещения до оси изделия, у декора — до центра.
2. Красные цепочки — привязки электроточек и выводов: по горизонтали от угла чистовых стен, по вертикали от чистого пола, до оси изделия; звенья короче 3 мм на листе вынесены во второй ярус (ближние к стене цепочка).
3. У знака электроточки: марка (Р — розетка, S — выключатель, Св — светильник, ЭВ — вывод кабеля), ×N — число постов в рамке, гр. — группа щита, Н — высота оси от чистого пола, мм; группы по клавишам выключателя — на листе выключателей.
4. Схема мебели, приборов и декора не является технической документацией для производства мебели; габариты — по паспортам изделий.
5. Картины и зеркала крепить к основанию по паспорту изделия (закладные и анкеры — в перечне скрытых работ); крест — ось центра предмета.
6. Двери скрытого монтажа — полотно в плоскости стены, отделка стены по полотну, плинтус прерывается у короба (узел — на листе узлов).
7. Потолок на развёртках — по нижнему уровню У1; другие уровни потолка помещения: У2 +2,600.

1000 мм · печать 1:1

| Изм. | Кол.уч | Лист | № док. | Подп. | Дата |
|---|---|---|---|---|---|
| Разраб. | | Кырпан А.С. | | | 05.10.26 |
| Пров. | | | | | |
| ГИП | | | | | |
| | | | | | |
| Н. контр. | | | | | |
| Утв. | | | | | |

**ГД-2026-003-АИ**

Трёхкомнатная квартира

Общая площадь 78,95* м² · * размеры со скана, не замерены (реестр — п. 6–11, К-13)

Дизайн-проект интерьера трёхкомнатной квартиры

| Стадия | Лист | Листов |
|---|---|---|
| РП | 81 | 94 |

**Развёртки стен В2, Г1, Г2. Кухня-гостиная (пом. 6)**

М 1:40

Кырпан Александр Сергеевич

выпуск 05.10.2026 № 6add39ab8d · стр. 92 из 137

# Развёртки стен А, Б. Санузел 2 (пом. 7)

Санузел 2 (пом. 7) · вид изнутри помещения · размеры в мм, отметки в м

## Развёртка стены А

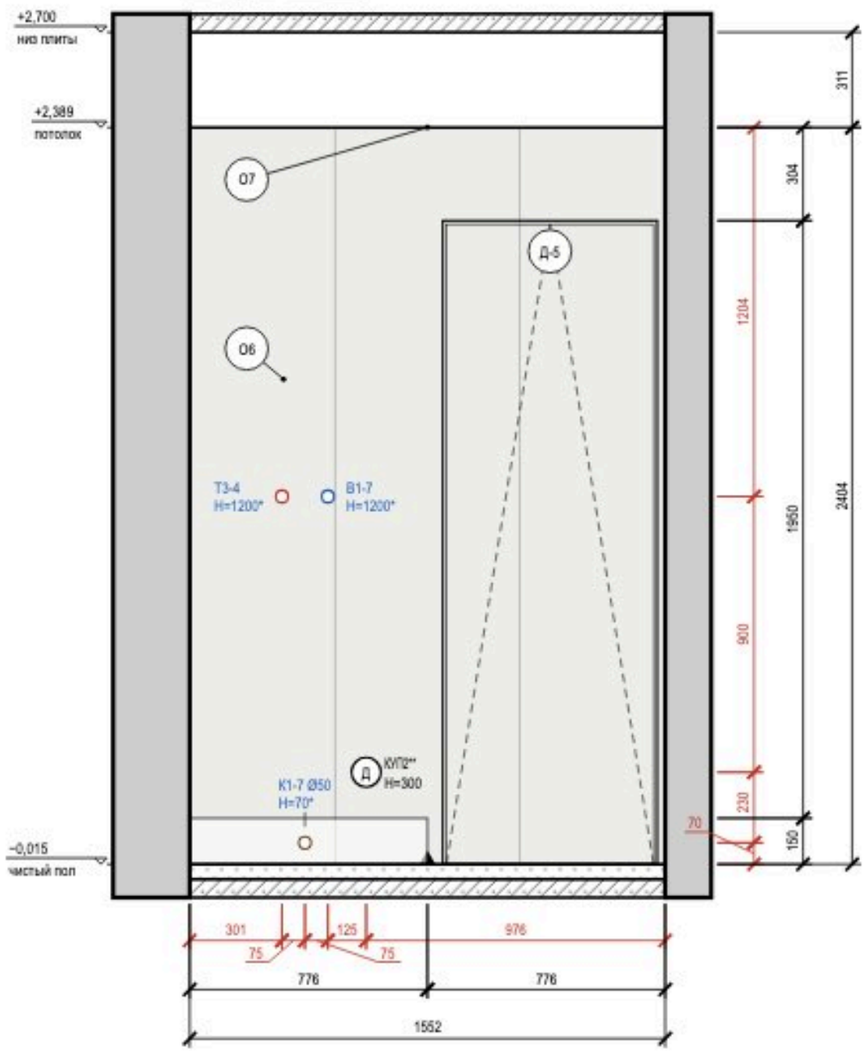


## Развёртка стены Б

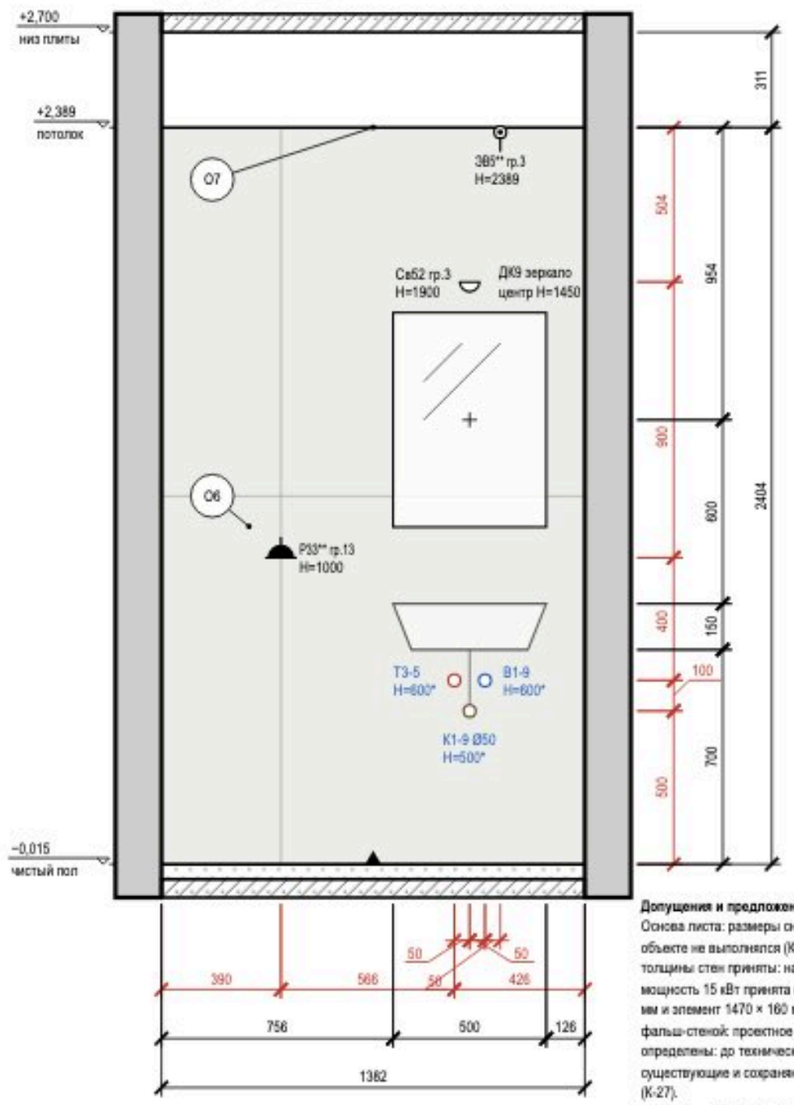


## Схема развёрток (М 1:100)

## Условные обозначения

- розетка влагозащищённая IP44
- вывод кабеля для подключения прибора (без розетки), марка ЭВ
- светильник настенный (бра), Н — высота оси
- вывод В1 (код — в ведомости привязок)
- вывод Т3 (код — в ведомости привязок)
- вывод К1 (код — в ведомости привязок)
- привязки точек и выводов от угла и от пола, мм
- мебель и приборы — фасад по расстановке (условно)
- зеркало: марка Д, крест — центр, Н — высота центра, мм
- дверь скрытого монтажа: полотно в плоскости стены (узел — на листе узлов)
- стены и перекрытия в сечении
- плитка: сетка швов по формату, ▲ — ось старта
- О1 — марка отделки по реестру отделки альбома
- А — марка развёртки: буква стены, стрелка — взгляд

**Допущения и предложения на листе**

Основа листа: размеры сняты со скана плана заказчика по размерным цепочкам, контрольный обмер на объекте не выполнялся (К-13); высота потолка 2700 мм принята: на плане заказчика не указана (К-11); толщины стен приняты: наружные 250 мм, перегородки 150 мм (на плане 85–190 мм) (К-13); разрешённая мощность 15 кВт принята по типовой квартире, технических условий нет (К-14); утолщение стены 190 × 1360 мм и элемент 1470 × 160 мм плана заказчика не определены (К-12); ниша санузла 2 закрыты перегородкой и фальш-стеной: проектное решение, на плане заказчика ниша у входа открыта (К-18); несущие стены не определены: до технического заключения все существующие стены считаются несущими (К-20); окна существующие и сохраняются; подоконная доска и глубина откосов не заданы — приняты, не замерены (К-27).

Знак «*» — принято, не замерено и не подтверждено (замерить на объекте): К-13: отметка существующего пола — отметка существующего пола и верха плиты не замерена: на плане заказчика отметок нет; нивелировка — в задании на обмер (К-13).

Знак «**» — предложение проектировщика, заказчиком не утверждено (согласовать с заказчиком): ИЗ-4, ИЗ-9, К-7: Р33; ИЗ-8: ЭВ5 — вывод к бытовому вентилятору, таймер выбега; КУП2 — коробка уравнивания потенциалов, проводник от шины РЕ.

См. лист открытых вопросов (лист 6, записи К-7, К-11; лист 7, записи К-12–К-14, К-18, К-20; лист 8, запись К-27; лист 9, записи ИЗ-4, ИЗ-8, ИЗ-9).

## Примечания

1. Развёртки — вид на стену изнутри помещения, по часовой стрелке; расположение — на схеме листа и на листе 68; размеры — в мм по чистовым поверхностям; отметки — в м от ±0,000; высоты Н — от чистого пола помещения до оси изделия, у декора — до центра.
2. Красные цепочки — привязки электроточек и выводов: по горизонтали от угла чистовых стен, по вертикали от чистого пола, до оси изделия; звенья короче 3 мм на листе вынесены во второй ярус (ближняя к стене цепочка).
3. У знака электроточки: марка (Р — розетка, S — выключатель, Св — светильник, ЭВ — вывод кабеля), ×N — число постов в рамке, гр. — группа щита, Н — высота оси от чистого пола, мм; группы по клавишам выключателя — на листе выключателей.
4. Схема мебели, приборов и декора не является технической документацией для производства мебели; габариты — по паспортам изделий (* — высота не задана в проекте, показана по типовому изделию).
5. Выводы ВК — коды и высоты по листу выводов сантехники; * — высота принята по типовой практике монтажа, окончательно — по паспорту прибора.
6. Облицовка — по сетке швов 2 мм, раскладка от оси стены (треугольник у пола), целые ряды от пола; подрезки — по листу раскладки плитки.
7. Гидроизоляция в 2 слоя, заход на стены 200 мм — до облицовки, с актом скрытых работ и тестом проливом (узел — на листе узлов).
8. Картины и зеркала крепить к основанию по паспорту изделия (закладные и анкеры — в перечне скрытых работ); крест — ось центра предмета.
9. Двери скрытого монтажа — полотно в плоскости стены, отделка стены по полотну, плинтус прерывается у короба (узел — на листе узлов).

1000 мм · печать 1:1

| | | | | | | | |
|---|---|---|---|---|---|---|---|
| | | | | | | ГД-2026-003-АИ | |
| | | | | | | Трёхкомнатная квартира | |
| | | | | | | Общая площадь 78,95* м² · * размеры со скана, не замерены (реестр — п. 6–11, К-13) | |
| Изм. | Кол.уч | Лист | № док. | Подп. | Дата | Дизайн-проект интерьера трёхкомнатной квартиры | Стадия: РП; Лист: 82; Листов: 94 |
| Разраб. | | Кырпан А.С. | | | 05.10.26 | | |
| Пров. | | | | | | | |
| ГИП | | | | | | | |
| | | | | | | Развёртки стен А, Б. Санузел 2 (пом. 7) | Кырпан Александр Сергеевич |
| Н. контр. | | | | | | М 1:20 | |
| Утв. | | | | | | | |

выпуск 05.10.2026 · 6add39ab8d · стр. 93 из 137

# Развёртки стен В, Г. Санузел 2 (пом. 7)

Санузел 2 (пом. 7) · вид изнутри помещения · размеры в мм, отметки в м

ПРЕДВАРИТЕЛЬНО · не для производства работ · открыто пунктов: 31 (реестр — п. 6–11)

### Развёртка стены В

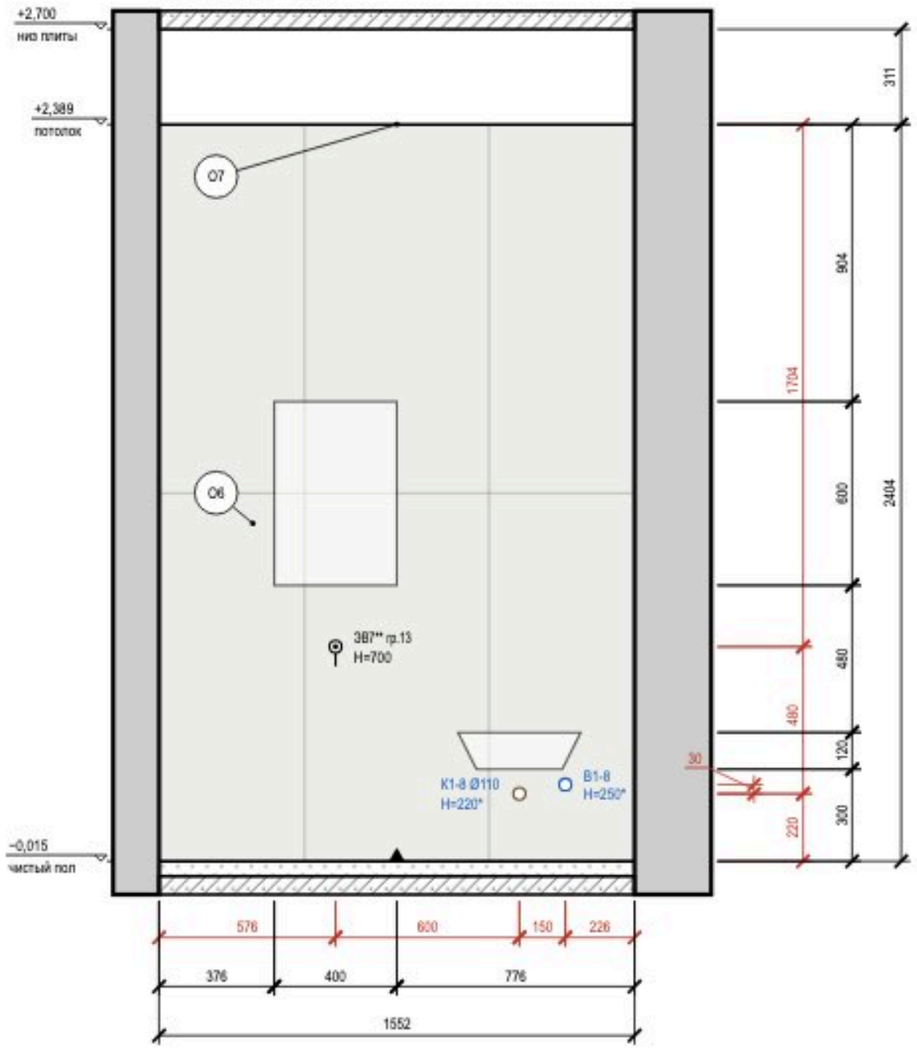


### Развёртка стены Г

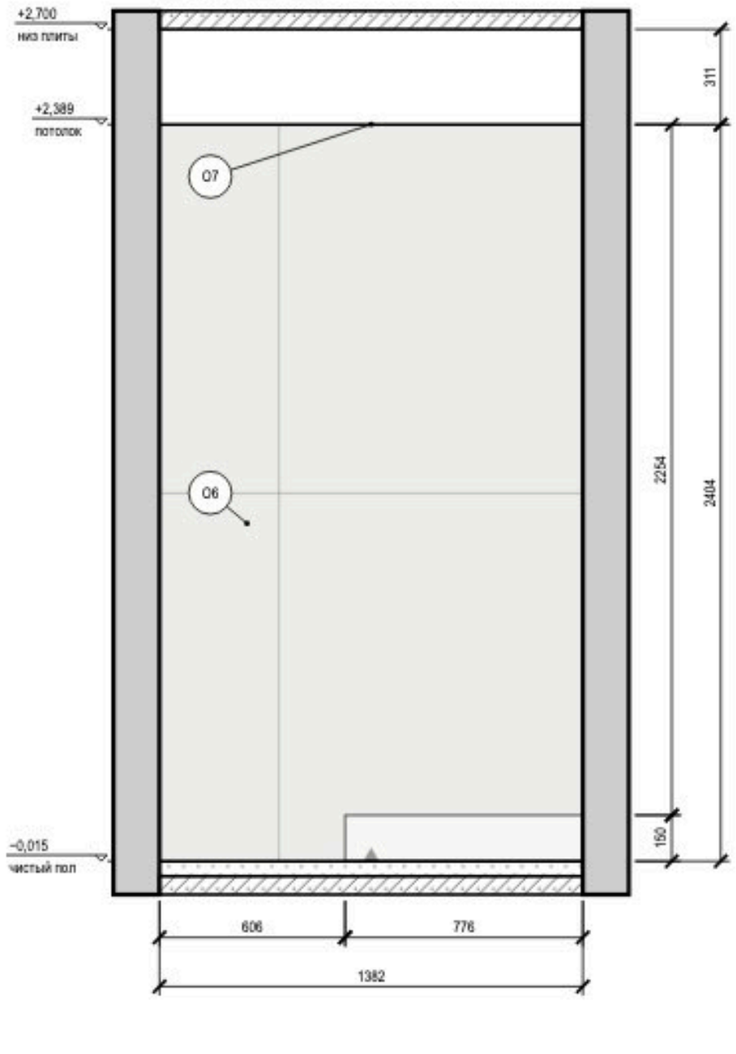


### Схема развёрток (М 1:100)

### Условные обозначения

- вывод кабеля для подключения прибора (без розетки), марка ЭВ
- вывод В1 (код — в ведомости привязок)
- вывод К1 (код — в ведомости привязок)
- привязки точек и выводов от угла и от пола, мм
- мебель и приборы — фасад по расстановке (условно)
- стены и перекрытия в сечении
- плитка: сетка швов по формату, ▲ — ось старта
- О1 — марка отделки по реестру отделки альбома
- А — марка развёртки: буква стены, стрелка — взгляд

**Допущения и предложения на листе**

Основа листа: размеры сняты со скана плана заказчика по размерным цепочкам, контрольный обмер на объекте не выполнялся (К-13); высота потолка 2700 мм принята: на плане заказчика не указана (К-11); толщины стен приняты: наружные 250 мм, перегородки 150 мм (на плане 85–190 мм) (К-13); разрешённая мощность 15 кВт принята по типовой квартире, технических условий нет (К-14); утолщение стены 190 × 1360 мм и элемент 1470 × 160 мм плана заказчика не определены (К-12); ниши санузла 2 закрыты перегородкой и фальш-стенкой: проектное решение, на плане заказчика ниша у входа открыта (К-18); несущие стены не определены: до технического заключения все существующие стены считаются несущими (К-20); окна существующие и сохраняются; подоконная доска и глубина откосов не заданы — приняты, не замерены (К-27).

Знак «*» — принято, не замерено и не подтверждено (замерить на объекте): К-13: отметка существующего пола — отметка существующего пола и верха плиты не замерена: на плане заказчика отметок нет; нивелировка — в задании на обмер (К-13).

Знак «**» — предложение проектировщика, заказчиком не утверждено (согласовать с заказчиком): ИЗ-1: ЭВ7.

См. лист открытых вопросов (лист 6, запись К-11; лист 7, записи К-12–К-14, К-18, К-20; лист 8, запись К-27; лист 9, запись ИЗ-1).

## Примечания

1. Развёртки — вид на стену изнутри помещения, по часовой стрелке; расположение — на схеме листа и на листе 68; размеры — в мм по чистовым поверхностям; отметки — в м от ±0,000; высоты Н — от чистого пола помещения до оси изделия, у декора — до центра.
2. Красные цепочки — привязки электроточек и выводов: по горизонтали от угла чистовых стен, по вертикали от чистого пола, до оси изделия; звенья короче 3 мм на листе вынесены во второй ярус (ближняя к стене цепочка).
3. У знака электроточки: марка (Р — розетка, S — выключатель, Св — светильник, ЭВ — вывод кабеля), ×N — число постов в рамке, гр. — группа щита, Н — высота оси от чистого пола, мм; группы по клавишам выключателя — на листе выключателей.
4. Схема мебели, приборов и декора не является технической документацией для производства мебели; габариты — по паспортам изделий (* — высота не задана в проекте, показана по типовому изделию).
5. Выводы ВК — коды и высоты по листу выводов сантехники; * — высота принята по типовой практике монтажа, окончательно — по паспорту прибора.
6. Облицовка — по сетке швов 2 мм, раскладка от оси стены (треугольник у пола), целые ряды от пола; подрезки — по листу раскладки плитки.
7. Гидроизоляция в 2 слоя, заход на стены 200 мм — до облицовки, с актом скрытых работ и тестом проливом (узел — на листе узлов).

1000 мм · печать 1:1

| Изм. | Кол.уч | Лист | № док. | Подп. | Дата |
|---|---|---|---|---|---|
| Разраб. | | Кырпан А.С. | | | 05.10.26 |
| Пров. | | | | | |
| ГИП | | | | | |
| | | | | | |
| Н. контр. | | | | | |
| Утв. | | | | | |

**ГД-2026-003-АИ**

Трёхкомнатная квартира

Общая площадь 78,95* м² · * размеры со скана, не замерены (реестр — п. 6–11, К-13)

Дизайн-проект интерьера трёхкомнатной квартиры

| Стадия | Лист | Листов |
|---|---|---|
| РП | 83 | 94 |

**Развёртки стен В, Г. Санузел 2 (пом. 7)**

М 1:20

**Кырпан Александр Сергеевич**

выпуск 05.10.2026 · 6add39ab8d · стр. 94 из 137

# Развёртки стен А, Б, В. Коридор (пом. 8)

Коридор (пом. 8) · вид изнутри помещения · размеры в мм, отметки в м

ПРЕДВАРИТЕЛЬНО · не для производства работ · открыто пунктов: 31 (реестр — л. 6–11)

### Развёртка стены А

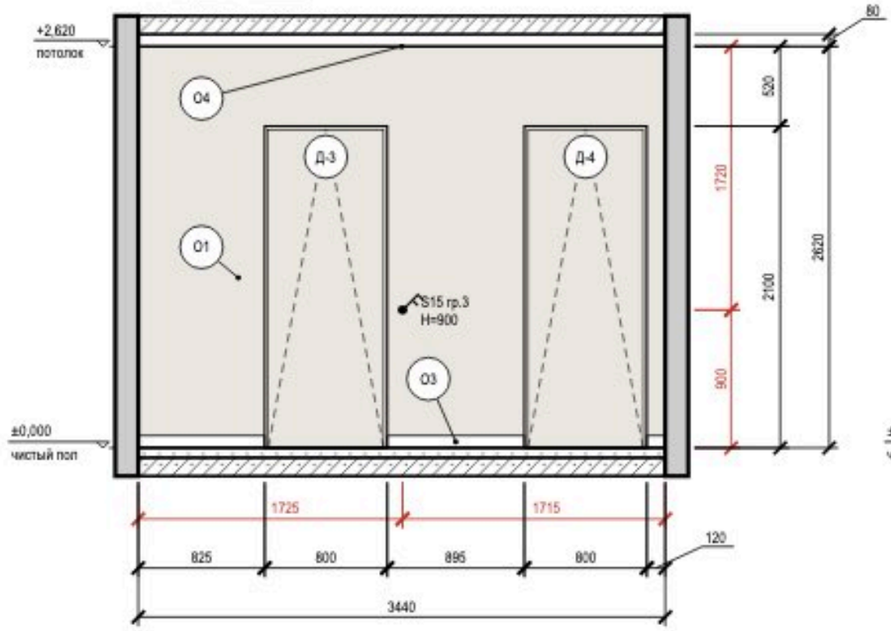


### Развёртка стены Б

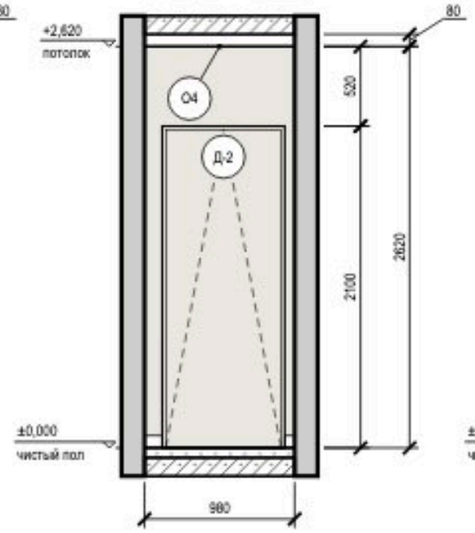


### Развёртка стены В

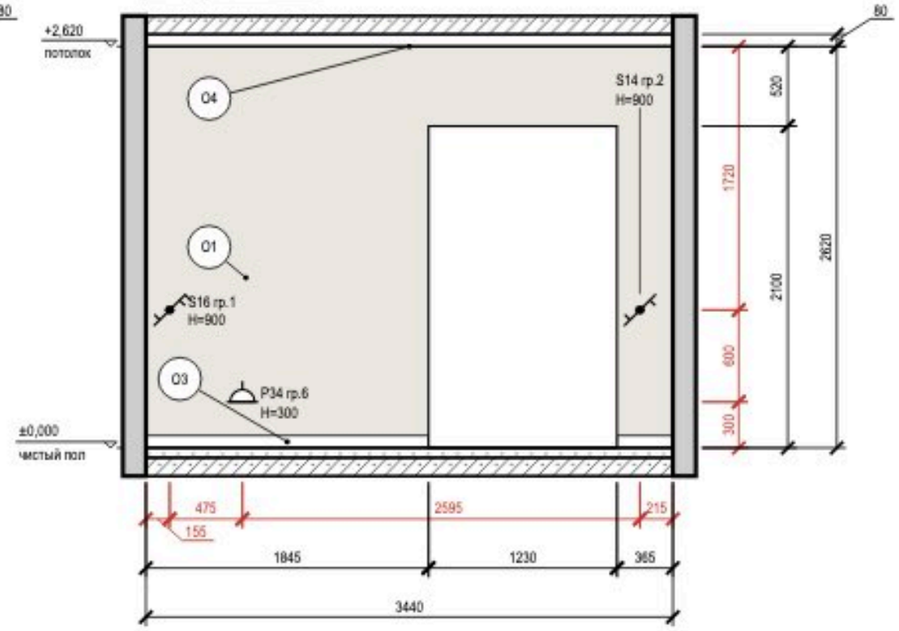


### Схема развёрток (М 1:100)

### Условные обозначения

- розетка с заземляющим контактом; у знака — марка, ×N постов в рамке, гр. — группа щита, H — высота оси, мм
- выключатель одноклавишный
- выключатель двухклавишный (флажков — по числу клавиш)
- выключатель с проходной или перекрёстной клавишей (обратный флажок); тип клавиши — в подписи
- привязки точек и выводов от угла и от пола, мм
- мебель и приборы — фасад по расстановке (условно)
- дверь скрытого монтажа: полотно в плоскости стены (узел — на листе узлов)
- дверной проём; марка двери — в кружке
- стены и перекрытия в сечении
- окраска: тон — цвет по коду производителя (условно)
- О1 — марка отделки по реестру отделки альбома
- А — марка развёртки: буква стены, стрелка — взгляд

### Ведомость отделки (на листе)

| Марка | Поверхность | Материал, изделие | Цвет, код | Кол. |
|---|---|---|---|---|
| О1 | стены | окраска, Farrow & Ball Modern Emulsion, матовая, подготовка Q3 | Farrow & Ball No. 241 «Skimming Stone» | 13 м² |
| О3 | плинтус | плинтус МДФ, h 80 мм, аналог: плинтус МДФ под покраску 80×16 | Farrow & Ball No. 241 «Skimming Stone» | 4,2 м |
| О4 | потолок | окраска, Tikkurila Anti-Reflex 2, глубокоматовая, подготовка Q3 | Tikkurila V503 «Winter» | 3,5 м² |

**Допущения и предложения на листе**

Основа листа: размеры сняты со скана плана заказчика по размерным цепочкам, контрольный обмер на объекте не выполнялся (К-13); высота потолка 2700 мм принята: на плане заказчика не указана (К-11); толщины стен приняты: наружные 250 мм, перегородки 150 мм (на плане 85–190 мм) (К-13); разрешённая мощность 15 кВт принята по типовой квартире, технических условий нет (К-14); утолщение стены 190 × 1360 мм и элемент 1470 × 160 мм плана заказчика не определены (К-12); ниши санузла 2 закрыты перегородкой и фальш-стеной: проектное решение, на плане заказчика ниша у входа открыта (К-18); несущие стены не определены: до технического заключения все существующие стены считаются несущими (К-20); окна существующие и сохраняются; подоконная доска и глубина откосов не заданы — приняты, не замерены (К-27).

Знак «*» — принято, не замерено и не подтверждено (замерить на объекте): К-13: отметка существующего пола — отметка существующего пола и верха плиты не замерена: на плане заказчика отметок нет; нивелировка — в задании на обмер (К-13); К-25: дверь пом. 8 (стена А) — толщина стены в проёме принята 150 мм (как у всех перегородок модели), по скану плана заказчика стена 85 мм — не замерено (К-25); проём существующий, скрытый блок ставится в него с зазором 10–15 мм на сторону, полотно уже проёма; узел скрытой двери выполнен для принятой толщины 150 мм.

См. лист открытых вопросов (лист 6, запись К-11; лист 7, записи К-12–К-14, К-18, К-20; лист 8, записи К-25, К-27).

### Примечания

1. Развёртки — вид на стену изнутри помещения, по часовой стрелке; расположение — на схеме листа и на листе 68; размеры — в мм по чистовым поверхностям; отметки — в м от ±0,000; высоты H — от чистого пола помещения до оси изделия, у декора — до центра.
2. Красные цепочки — привязки электроточек и выводов: по горизонтали от угла чистовых стен, по вертикали от чистого пола, до оси изделия; звенья короче 3 мм на листе вынесены во второй ярус (ближняя к стене цепочка).
3. У знака электроточки: марка (Р — розетка, S — выключатель, Св — светильник, ЭВ — вывод кабеля), ×N — число постов в рамке, гр. — группа щита, H — высота оси от чистого пола, мм; группы по клавишам выключателя — на листе выключателей.
4. Схема мебели, приборов и декора не является технической документацией для производства мебели; габариты — по паспортам изделий.
5. Двери скрытого монтажа — полотно в плоскости стены, отделка стены по полотну, плинтус прерывается у короба (узел — на листе узлов).

1000 мм · печать 1:1

| Изм. | Кол.уч | Лист | № док. | Подп. | Дата |
|---|---|---|---|---|---|
| Разраб. | | Кырпан А.С. | | | 05.10.26 |
| Пров. | | | | | |
| ГИП | | | | | |
| | | | | | |
| Н. контр. | | | | | |
| Утв. | | | | | |

**ГД-2026-003-АИ**

Трёхкомнатная квартира

Общая площадь 78,95* м² · * размеры со скана, не замерены (реестр — п. 6–11, К-13)

Дизайн-проект интерьера трёхкомнатной квартиры

| Стадия | Лист | Листов |
|---|---|---|
| РП | 84 | 94 |

Развёртки стен А, Б, В. Коридор (пом. 8)

М 1:40

Кырпан Александр Сергеевич

выпуск 05.10.2026 · 6add39ab8d · стр. 95 из 137

# Развёртка стены Г. Коридор (пом. 8)

Коридор (пом. 8) · вид изнутри помещения · размеры в мм, отметки в м

ПРЕДВАРИТЕЛЬНО · не для производства работ · открыто пунктов: 31 (реестр — л. 6–11)

### Развёртка стены Г

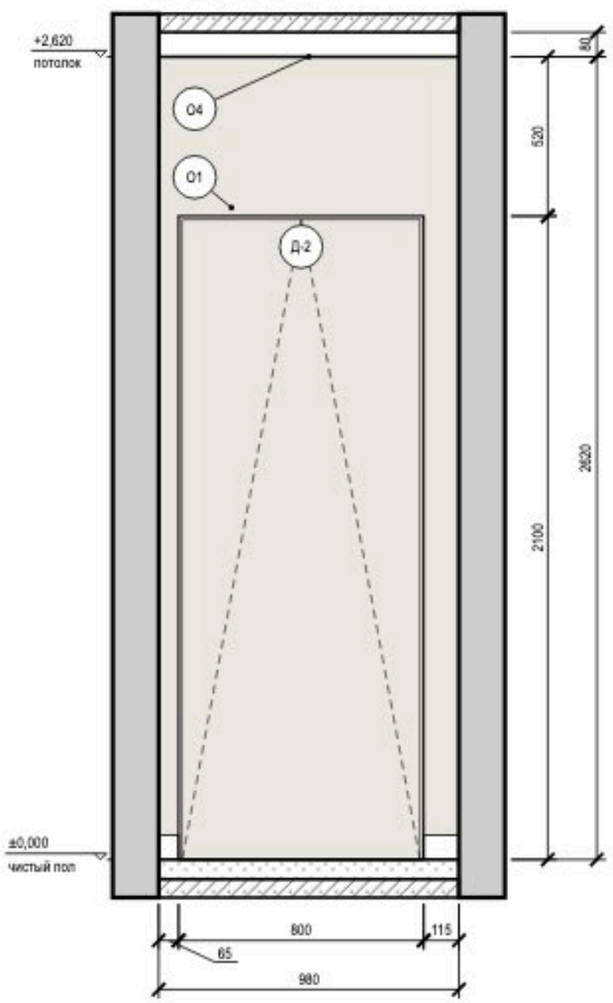


### Схема развёрток (М 1:100)

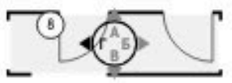


### Условные обозначения

привязки точек и выводов от угла и от пола, мм

мебель и приборы — фасад по расстановке (условно)

дверь скрытого монтажа: полотно в плоскости стены (узел — на листе узлов)

стены и перекрытия в сечении

окраска: тон — цвет по коду производителя (условно)

О1 — марка отделки по реестру отделки альбома

А — марка развёртки: буква стены, стрелка — взгляд

### Ведомость отделки (на листе)

| Марка | Поверхность | Материал, изделие | Цвет, код | Кол. |
|---|---|---|---|---|
| О1 | стены | окраска, Farrow & Ball Modern Emulsion, матовая, подготовка Q3 | Farrow & Ball No. 241 «Skimming Stone» | 0,9 м² |
| О3 | плинтус | плинтус МДФ, h 80 мм, аналог: плинтус МДФ под покраску 80×16 | Farrow & Ball No. 241 «Skimming Stone» | 0,2 м |
| О4 | потолок | окраска, Tikkurila Anti-Reflex 2, глубокоматовая, подготовка Q3 | Tikkurila V503 «Winter» | 3,5 м² |

**Допущения и предложения на листе**

Основа листа: размеры сняты со скана плана заказчика по размерным цепочкам, контрольный обмер на объекте не выполнялся (К-13); высота потолка 2700 мм принята: на плане заказчика не указана (К-11); толщины стен приняты: наружные 250 мм, перегородки 150 мм (на плане 85–190 мм) (К-13); разрешённая мощность 15 кВт принята по типовой квартире, технических условий нет (К-14); утолщение стены 190 × 1360 мм и элемент 1470 × 160 мм плана заказчика не определены (К-12); ниши санузла 2 закрыты перегородкой и фальш-стеной: проектное решение, на плане заказчика ниша у входа открыта (К-18); несущие стены не определены: до технического заключения все существующие стены считаются несущими (К-20); окна существующие и сохраняются; подоконная доска и глубина откосов не заданы — приняты, не замерены (К-27).

Знак «*» — принято, не замерено и не подтверждено (замерить на объекте): К-13: отметка существующего пола — отметка существующего пола и верха плиты не замерена: на плане заказчика отметок нет; нивелировка — в задании на обмер (К-13); К-25: дверь пом. 8 (стена А) — толщина стены в проёме принята 150 мм (как у всех перегородок модели), по скану плана заказчика стена 85 мм — не замерено (К-25); проём существующий, скрытый блок ставится в него с зазором 10–15 мм на сторону, полотно уже проёма; узел скрытой двери выполнен для принятой толщины 150 мм. См. лист открытых вопросов (лист 6, запись К-11; лист 7, записи К-12–К-14, К-18, К-20; лист 8, записи К-25, К-27).

## Примечания

1. Развёртки — вид на стену изнутри помещения, по часовой стрелке; расположение — на схеме листа и на листе 68; размеры — в мм по чистовым поверхностям; отметки — в м от ±0,000; высоты Н — от чистого пола помещения до оси изделия, у декора — до центра.
2. Красные цепочки — привязки электроточек и выводов: по горизонтали от угла чистовых стен, по вертикали от чистого пола, до оси изделия; звенья короче 3 мм на листе вынесены во второй ярус (ближняя к стене цепочка).
3. У знака электроточки: марка (Р — розетка, S — выключатель, Св — светильник, ЭВ — вывод кабеля), ×N — число постов в рамке, гр. — группа щита, Н — высота оси от чистого пола, мм; группы по клавишам выключателя — на листе выключателей.
4. Схема мебели, приборов и декора не является технической документацией для производства мебели; габариты — по паспортам изделий.
5. Двери скрытого монтажа — полотно в плоскости стены, отделка стены по полотну, плинтус прерывается у короба (узел — на листе узлов).

1000 мм · печать 1:1

| Изм. | Кол.уч | Лист | № док. | Подп. | Дата |
|---|---|---|---|---|---|
| Разраб. | | Кырпан А.С. | | | 05.10.26 |
| Пров. | | | | | |
| ГИП | | | | | |
| | | | | | |
| Н. контр. | | | | | |
| Утв. | | | | | |

**ГД-2026-003-АИ**

Трёхкомнатная квартира

Общая площадь 78,95* м² · * размеры со скана, не замерены (реестр — п. 6–11, К-13)

| Дизайн-проект интерьера трёхкомнатной квартиры | Стадия | Лист | Листов |
|---|---|---|---|
| | РП | 85 | 94 |
| **Развёртка стены Г. Коридор (пом. 8)** М 1:20 | **Кырпан Александр Сергеевич** | | |

выпуск 05.10.2026 № 6add39ab8d · стр. 96 из 137

# Узлы

Пороги и стыки покрытий, скрытые двери, короба стояков, гидроизоляция, плинтус

### 1 Порог 15 мм: мокрая зона — жилое помещение (М 1:10)

Применение: двери Д-5, Д-3; места — лист 68

### 2 Стык покрытий пола Т-профилем без перепада (М 1:5)

Применение: проёмы 5↔6, 8↔5; места — лист 68

### 3 Дверь скрытого монтажа в плоскости стены, плинтус (М 1:5)

Применение: двери Д-2, Д-5, Д-3, Д-4; места — лист 68

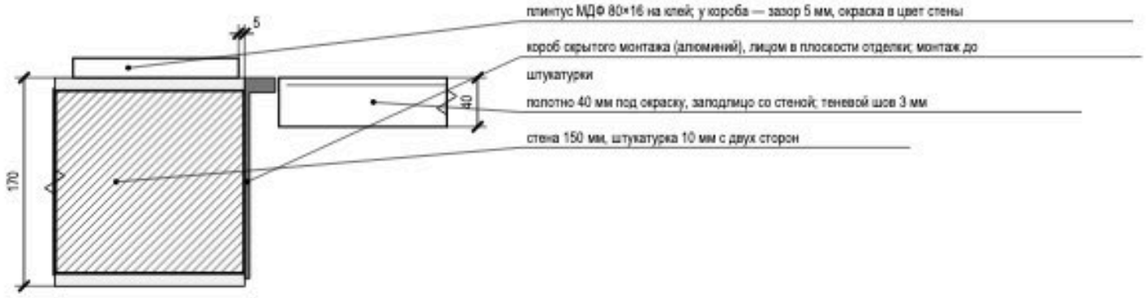


### 4 Короб стояков К1-1, В1-1 с люком и звукоизоляцией (М 1:20)

Применение: пом. 2; места — лист 68

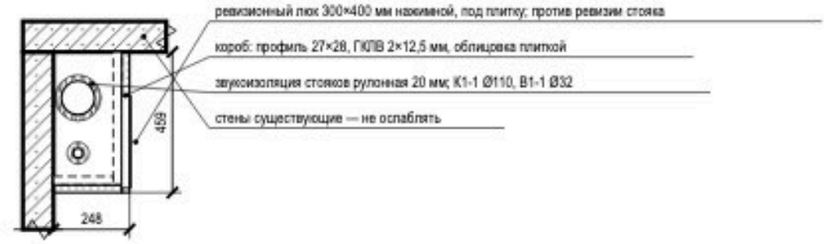


### 5 Гидроизоляция санузла: заход на стены 200 мм, примыкание ванны (М 1:20)

Применение: пом. 2, 7; места — лист 68

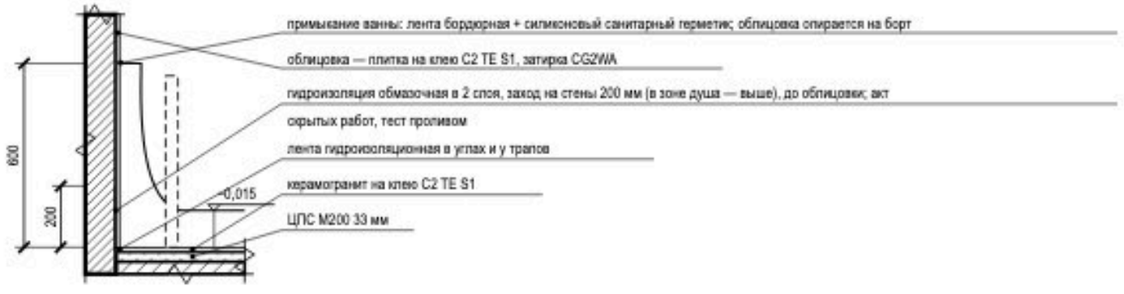


### 6 Плинтус МДФ 80×16 мм у окрашенной стены (М 1:10)

Применение: пом. 1, 3, 4, 5, 6, 8; места — лист 68

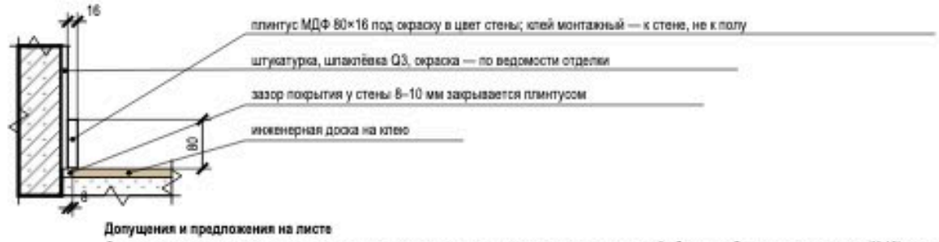


## Условные обозначения

- железобетон (плита, стены)
- кладка, перегородка
- стяжка, раствор
- гипсокартон ГКЛВ
- звукоизоляция, эластичный заполнитель
- плитка, керамогранит на клею
- инженерная доска (покрытие пола)
- металлический профиль (порог, Т-профиль, короб двери)
- гидроизоляция (обмазочная, лента)

## Примечания

1. Узлы — типовые решения проекта для мест, отмеченных выносками на листе схемы расположения развёрток и узлов; размеры — в мм, отметки — в м от ±0,000.
2. Узлы с гидроизоляцией, закладными и коробами скрытого монтажа принимаются по актам скрытых работ до закрытия отделкой; гидроизоляция — после теста проливом (24 ч).
3. Марки изделий (порог, Т-профиль, короб скрытой двери, люк) — по спецификациям; замена — на аналог с теми же габаритами по согласованию с автором проекта.

**Допущения и предложения на листе**

Основа листа: размеры сняты со скана плана заказчика по размерным цепочкам, контрольный обмер на объекте не выполнялся (К-13); высота потолка 2700 мм принята: на плане заказчика не указана (К-11); толщины стен приняты: наружные 250 мм, перегородки 150 мм (на плане 85–190 мм) (К-13); разрешённая мощность 15 кВт принята по типовой квартире, технических условий нет (К-14); утолщение стены 190 × 1360 мм и элемент 1470 × 160 мм плана заказчика не определены (К-12); ниши санузла 2 закрыты перегородкой и фальш-стеной: проектное решение, на плане заказчика ниша у входа открыта (К-18); несущие стены не определены: до технического заключения все существующие стены считаются несущими (К-20); окна существующие и сохраняются; подоконная доска и глубина откосов не заданы — приняты, не замерены (К-27).

Открытые вопросы и конфликты по листу: К-25.

Изменения по листу без подписи: ИЗ-16.

См. лист открытых вопросов (лист 6, запись К-11; лист 7, записи К-12–К-14, К-18, К-20; лист 8, записи К-25, К-27; лист 10, запись ИЗ-16).

| Изм. | Кол.уч | Лист | № док. | Подп. | Дата |
|---|---|---|---|---|---|
| Разраб. | | Кырпан А.С. | | | 05.10.26 |
| Пров. | | | | | |
| ГИП | | | | | |
| | | | | | |
| Н. контр. | | | | | |
| Утв. | | | | | |

**ГД-2026-003-АИ**

Трёхкомнатная квартира

Общая площадь 78,95* м² · * размеры со скана, не замерены (реестр — п. 6–11, К-13)

Дизайн-проект интерьера трёхкомнатной квартиры

| Стадия | Лист | Листов |
|---|---|---|
| РП | 86 | 94 |

**Узлы**

М 6/м

Кырпан Александр Сергеевич

выпуск 05.10.2026 · 6add39ab8d · стр. 97 из 137

10

# Смета

Кырлан Александр Сергеевич

выпуск 05.10.2026 № 6add39ab8d · стр. 98 из 137

# Ведомость объёмов работ

ПРЕДВАРИТЕЛЬНО · не для производства работ · открыто пунктов: 31 (реестр — л. 6–11)

Объёмы по помещениям от чертежа · площади в м², длины в м · формула, правило проёмов и источник в каждой строке

## Ведомость объёмов работ по помещениям

| Поз. | Наименование работ (материал, число слоёв) | Ед. изм. | Объём по помещениям (№ по экспликации) | | | | | | | | Всего | Формула подсчёта | Правило проёмов | Источник | Цена за ед., ₽ | Стоимость, ₽ |
|---|---|---|---|---|---|---|---|---|---|---|---|---|---|---|---|---|
| | | | 1 | 2 | 3 | 4 | 5 | 6 | 7 | 8 | | | | | | |
| **1. Демонтаж и черновые работы** | | | | | | | | | | | | | | | | |
| 1 | Демонтаж существующего покрытия пола до основания | м² | 17,75 | 4,43 | 1,85 | 12,80 | 7,13 | 29,20 | 2,29 | 3,50 | 78,95 | S пом. | | л. 21–23 | по КП | |
| 2 | Демонтаж существующей отделки стен до основания | м² | 39,17 | 18,61 | 14,74 | 32,44 | 21,86 | 51,56 | 13,10 | 14,17 | 205,65 | P × H − проёмы | за вычетом проёмов | л. 21–23 | по КП | |
| 3 | Демонтаж существующей отделки потолка до основания | м² | 17,75 | 4,43 | 1,85 | 12,80 | 7,13 | 29,20 | 2,29 | 3,50 | 78,95 | S пом. | | л. 21–23 | по КП | |
| 4 | Демонтаж существующих дверных блоков | шт | 1 | | | 1 | 1 | 1 | | 2 | 6 | по ведомости проёмов | | л. 22–24 | по КП | |
| 5 | Демонтаж существующих сантехприборов и электрооборудования (если есть) | компл | | | | | | | | | | по факту на объекте | | л. 22, 23 | по КП | |
| 6 | Монтаж каркасной перегородки П-1** (С112): каркас ПС усиленный через 400 мм, ГКЛВ в 2 слоя с каждой стороны, обрамление проёма профилем УА; предложение, пока П-1** не утверждена автором (К-18, К-4) | м² | | | | | | | | | 2,85 | 1,60 × 2,70 − 1,47 (Д-5 700 × 2100) = 2,85 м², одна сторона; пом. 6, 7 | проёмы вычтены | л. 22, 23, 43 | 2 700 | 7 695 |
| 7 | Облицовка (фальш-стена) П-2**: ГКЛВ в 2 слоя по раме инсталляции под плитку; предложение, пока П-2** не утверждена автором (К-18) | м² | | | | | | | | | 1,58 | 0,66 × 2,39 = 1,58 м², одна сторона; пом. 7 | проёмы вычтены | л. 22, 23, 43 | 1 050 | 1 659 |
| 8 | Заполнение каркаса П-1** минераловатной плитой (звукоизоляция, Rw 51 дБ); предложение, пока П-1** не утверждена автором (К-18, К-4) | м² | | | | | | | | | 2,85 | 2,85 м² без проёма | | л. 43 | по КП | |
| 9 | Шпаклёвка швов ГКЛВ П-1** под плитку (Q1), сторона санузла; предложение, пока П-1** не утверждена автором (К-18, К-4) | м² | | | | | | | | | 2,85 | 2,85 м² стороны, облицованной плиткой; сторона под окраску — в строке шпаклёвки стен помещения | | л. 43, 51 | по КП | |
| 10 | Шпаклёвка швов ГКЛВ П-2** под плитку (Q1), сторона санузла; предложение, пока П-2** не утверждена автором (К-18) | м² | | | | | | | | | 1,58 | 1,58 м² стороны, облицованной плиткой; сторона под окраску — в строке шпаклёвки стен помещения | | л. 43, 51 | по КП | |
| 11 | Устройство стяжки: стяжка ЦПС М200, 50 мм | м² | 17,81 | 4,49 | 1,91 | 12,86 | 7,45 | 29,37 | 2,34 | 3,63 | 80,06 | S пом. + S в дверных проёмах (b × h/2) | проёмы добавлены | л. 50, 51 | 530 | 42 432 |
| 12 | Гидроизоляция обмазочная, 2 слоя: пол, стены на 200 мм, зоны замачивания | м² | | 10,95 | | | | | 7,20 | | 18,15 | пол + (P − двери) × h заведения + зоны замачивания | | л. 46 | 450 | 8 167 |
| 13 | Штукатурка стен по маякам, до 10 мм | м² | 39,17 | 18,61 | 14,74 | 32,44 | 21,86 | 48,71 | 8,67 | 14,17 | 198,37 | P × H − проёмы по обводу коробок − грани перегородок на ГКЛВ | за вычетом проёмов | л. 21, 51 | 530 | 105 136 |
| 14 | Штукатурка оконных откосов шириной до 200 мм | м² | 0,92 | | | 0,78 | | 1,58 | | | 3,28 | Σ (2h + b) × глубина откоса | откосы ≤ 200 мм | л. 21 | 540 | 1 771 |
| 15 | Потолок ГКЛ по каркасу П113, 1 слой | м² | 17,75 | 4,43 | | 12,80 | 7,13 | 29,20 | 2,29 | 3,50 | 77,10 | S пом. по плану потолков | | л. 44, 45 | 1 500 | 115 650 |
| **Итого по разделу 1 — 282 510 ₽ (позиций 15, из них по КП 8); в сводную смету — л. 93, 94** | | | | | | | | | | | | | | | | |
| **2. Инженерные системы** | | | | | | | | | | | | | | | | |
| 16 | Прокладка кабеля ВВГнг(А)-LS по группам щита: за потолком и в штробах стен (штробы — только после технического заключения, см. строку «Штробы в стенах») | м | | | | | | | | | 377,00 | Σ длин групп щита | | л. 34 | 60 | 22 620 |
| 17 | Прокладка слаботочной линии: Кабель домофона — тип по системе поставщика, отдельно от силовых | м | | | | | | | | | 2,90 | по лучам от ЩС**: 1 точ., запас 10 % | | л. 36 | по КП | |
| 18 | Прокладка слаботочной линии: Кабель коаксиальный RG-6 (75 Ом) к розеткам ТВ, отдельно от силовых | м | | | | | | | | | 29,10 | по лучам от ЩС**: 2 точ., запас 10 % | | л. 36 | по КП | |
| 19 | Прокладка слаботочной линии: Кабель U/UTP кат. 6 (LAN, Wi-Fi и камеры по PoE), отдельно от силовых | м | | | | | | | | | 61,20 | по лучам от ЩС**: 5 точ., запас 10 % | | л. 36 | по КП | |
| 20 | Прокладка гофротрубы Ø20 для слаботочных линий, отдельно от силовых | м | | | | | | | | | 83,90 | по длине лучей без участков в канале плинтуса (≈ 90 %) | | л. 36 | по КП | |

**Допущения и предложения на листе**

Основа листа: размеры сняты со скана плана заказчика по размерным цепочкам, контрольный обмер на объекте не выполнялся (К-13); высота потолка 2700 мм принята: на плане заказчика не указана (К-11); толщины стен приняты: наружные 250 мм, перегородки 150 мм (на плане 85–190 мм) (К-13); разрешённая мощность 15 кВт принята по типовой квартире, технических условий нет (К-14); утолщение стены 190 × 1360 мм и элемент 1470 × 160 мм плана заказчика не определены (К-12); ниши санузла 2 закрыты перегородкой и фальш-стеной: проектное решение, на плане заказчика ниша у входа открыта (К-18); несущие стены не определены: до технического заключения все существующие стены считаются несущими (К-20); окна существующие и сохраняются; подоконная доска и глубина откосов не заданы — приняты, не замерены (К-27).

Знак «**» — предложение проектировщика, заказчиком не утверждено (согласовать с заказчиком): ИЗ-17: ЩС — щит слаботочный: место и состав; К-4, К-18: П-1 — проектное решение исполнителя: на плане заказчика ниша у входа открыта в кухню-гостиную; конструкция не утверждена автором (вопрос К-18), положение и размеры сняты со скана (К-13); К-18: П-2 — проектное решение исполнителя: на плане заказчика у наружной стены уступ 660 × 260 мм; конструкция не утверждена автором (вопрос К-18).

Открытые вопросы и конфликты по листу: К-28.

См. лист открытых вопросов (лист 6, записи К-4, К-11; лист 7, записи К-12–К-14, К-18, К-20; лист 8, записи К-27, К-28; лист 11, запись ИЗ-17).

| Изм. | Кол.уч | Лист | № док. | Подп. | Дата |
|---|---|---|---|---|---|
| Разраб. | | Кырпан А.С. | | | 05.10.26 |
| Пров. | | | | | |
| ГИП | | | | | |
| | | | | | |
| Н. контр. | | | | | |
| Утв. | | | | | |

**ГД-2026-003-АИ**

Трёхкомнатная квартира

Общая площадь 78,95* м² · * размеры со скана, не замерены (реестр — п. 6–11, К-13)

Дизайн-проект интерьера трёхкомнатной квартиры

| Стадия | Лист | Листов |
|---|---|---|
| РП | 87 | 94 |

**Ведомость объёмов работ**

М 6/м

Кырпан Александр Сергеевич

# Ведомость объёмов работ (продолжение)

Объёмы по помещениям от чертежа · площади в м², длины в м · формула, правило проёмов и источник в каждой строке

## Ведомость объёмов работ по помещениям (продолжение)

| Поз. | Наименование работ (материал, число слоёв) | Ед. изм. | Объём по помещениям (№ по экспликации) | | | | | | | | Всего | Формула подсчёта | Правило проёмов | Источник | Цена за ед., ₽ | Стоимость, ₽ |
|---|---|---|---|---|---|---|---|---|---|---|---|---|---|---|---|---|
| | | | 1 | 2 | 3 | 4 | 5 | 6 | 7 | 8 | | | | | | |
| 21 | Сборка слаботочного щита ЩС**: корпус, патч-панель, подключение линий и питания 220 В; коммутатор и точки доступа — оборудование заказчика | шт | | | | | | | | | 1 | один щит | | л. 32, 33, 36 | по КП | |
| 22 | Электроточка: подрозетник в бетоне, розетка, выключатель, вывод | шт | 10 | 4 | | 11 | 8 | 25 | 3 | 4 | 65 | по ведомости электроточек | | л. 29, 32, 33 | 950 | 61 750 |
| 23 | Штробы в стенах под спуски кабеля к точкам — выполняются только после технического заключения о несущих стенах | м | 18,00 | 4,53 | | 19,60 | 11,84 | 38,65 | 3,12 | 7,48 | 103,22 | Σ (H − h) по точкам на стенах: вертикальные спуски | после техзаключения | л. 22, 23, 29 | по КП | |
| 24 | Установка встраиваемого точечного светильника | шт | 8 | 3 | | 6 | 4 | 14 | 2 | 2 | 39 | по плану освещения | | л. 30 | 750 | 29 250 |
| 25 | Монтаж светильника: потолочного, подвесного, настенного | шт | 2 | 1 | 1 | 2 | | 3 | 1 | | 10 | по плану освещения | | л. 30 | 1 200 | 12 000 |
| 26 | Монтаж LED-ленты в алюминиевый профиль | м | 15,50 | | | 12,30 | 1,80 | 25,10 | | | 54,70 | Σ длин лент по плану освещения | | л. 30 | 230 | 12 581 |
| 27 | Установка блока питания LED в доступном месте (люк, шкаф) | шт | 1 | | | 1 | 1 | 2 | | | 5 | один на LED-группу | | л. 30 | 570 | 2 850 |
| 28 | Установка автономного пожарного извещателя | шт | 1 | | | 1 | 1 | 2 | | 1 | 6 | по плану розеток | | л. 29 | по КП | |
| 29 | Сборка щита: установка автоматов и АВДТ групп, вводного автомата | шт | | | | | | | | | 15 | группы + вводной автомат | | л. 34 | 230 | 3 450 |
| 30 | Установка вводного УЗО | шт | | | | | | | | | 1 | по однолинейной схеме | | л. 34 | 380 | 380 |
| 31 | Монтаж инсталляции, установка подвесного унитаза и кнопки смыва | шт | | 1 | | | | | 1 | | 2 | по плану выводов | | л. 39, 41 | 10 500 | 21 000 |
| 32 | Короб инсталляции: каркас и обшивка ГКЛВ в 2 слоя, ревизионный доступ к смыву | шт | | 1 | | | | | 1 | | 2 | по плану выводов | | л. 39, 46–49 | по КП | |
| 33 | Короб слояков Ш1 248 × 459 мм (внутренний 195 × 406): каркас и обшивка ГКЛВ в 2 слоя, ревизионный люк 300 × 400 | м² | | 1,70 | | | | | | | 1,70 | свободный периметр короба × H помещения | | л. 21, 39 | по КП | |
| 34 | Короб К1 над чистым полом: каркас и обшивка ГКЛВ под плитку (материалы — в спецификации ВК) | м.п. | | 0,85 | | | | | 1,32 | | 2,17 | Σ открытых участков выпусков К1 (профиль листа разводки ВК) | | л. 39, 41 | по КП | |
| 35 | Установка ванны с сифоном | шт | | 1 | | | | | | | 1 | по плану выводов | | л. 39, 41 | 6 000 | 6 000 |
| 36 | Установка умывальника (мойки) с сифоном и смесителем | шт | | 1 | | | | 1 | 1 | | 3 | по плану выводов | | л. 39, 41 | 3 000 | 9 000 |
| 37 | Установка душевого поддона с трапом, ограждения | шт | | | | | | | 1 | | 1 | по плану выводов | | л. 39, 41 | по КП | |
| 38 | Подключение стиральной (посудомоечной) машины к ВК | шт | | 1 | | | | 1 | | | 2 | по плану выводов | | л. 39 | по КП | |
| 39 | Установка радиатора с узлом подключения и терморегулятором | шт | 1 | | | 1 | | 2 | | | 4 | по плану отопления | | л. 38 | по КП | |
| **Итого по разделу 2 — 180 881 ₽ (позиций 24, из них по КП 13); в сводную смету — л. 93, 94** | | | | | | | | | | | | | | | | |
| **3. Чистовые работы** | | | | | | | | | | | | | | | | |
| 40 | Облицовка стен керамогранитом 600×1200 на клею | м² | | 17,65 | | | | | 12,38 | | 30,03 | по раскладке: зона облицовки − место за коробом | за вычетом проёмов | л. 46–49 | 2 500 | 75 075 |
| 41 | Облицовка короба инсталляции (ГКЛВ) керамогранитом: лицо, боковины, полка | м² | | 1,76 | | | | | 1,47 | | 3,23 | по раскладке: лицо, боковины, полка | | л. 46–49 | 2 500 | 8 075 |
| 42 | Облицовка фартука керамогранитом 1200×600 | м² | | | | | | 1,87 | | | 1,87 | по раскладке фартука | | л. 46–49, 51 | 2 400 | 4 488 |
| 43 | Укладка керамогранита на пол, 600×600, на клею | м² | | 4,49 | | | 7,45 | | 2,34 | | 14,28 | S пом. + S в дверных проёмах | проёмы добавлены | л. 46–50 | 1 800 | 25 704 |
| 44 | Затирка швов керамогранита | м² | | 23,84 | | | 7,13 | 1,87 | 16,14 | | 48,98 | Σ S облицовки и пола из плитки | | л. 46–49 | 150 | 7 347 |
| 45 | Грунтование стен, 2 слоя (под штукатурку и под отделку) | м² | 39,17 | 18,61 | 14,74 | 32,44 | 21,86 | 51,56 | 13,10 | 14,17 | 205,65 | P × H − проёмы | за вычетом проёмов | л. 51 | 96 | 19 742 |
| 46 | Шпаклёвка стен под окраску, 2 слоя (старт и финиш), уровень Q3 | м² | 39,17 | | 14,74 | 32,44 | 21,86 | 49,69 | | 14,17 | 172,07 | P × H − проёмы − фартук | за вычетом проёмов | л. 51 | 750 | 129 053 |
| 47 | Грунтование и шпаклёвка оконных откосов, 2 слоя | м.п. | 5,10 | | | 4,32 | | 8,77 | | | 18,19 | Σ (2h + b) по окнам | по окнам | л. 21 | 300 | 5 457 |

**Допущения и предложения на листе**

Основа листа: размеры сняты со скана плана заказчика по размерным цепочкам, контрольный обмер на объекте не выполнялся (К-13); высота потолка 2700 мм принята: на плане заказчика не указана (К-11); толщины стен приняты: наружные 250 мм, перегородки 150 мм (на плане 85–190 мм) (К-13); разрешённая мощность 15 кВт принята по типовой квартире, технических условий нет (К-14); утолщение стены 190 × 1360 мм и элемент 1470 × 160 мм плана заказчика не определены (К-12); ниши санузла 2 закрыты перегородкой и фальш-стеной: проектное решение, на плане заказчика ниша у входа открыта (К-18); несущие стены не определены: до технического заключения все существующие стены считаются несущими (К-20); окна существующие и сохраняются; подоконная доска и глубина откосов не заданы — приняты, не замерены (К-27).

Знак «**» — предложение проектировщика, заказчиком не утверждено (согласовать с заказчиком): ИЗ-17: ЩС — щит слаботочный: место и состав.

Открытые вопросы и конфликты по листу: К-28.

См. лист открытых вопросов (лист 6, запись К-11; лист 7, записи К-12–К-14, К-18, К-20; лист 8, записи К-27, К-28; лист 11, запись ИЗ-17).

| Изм. | Кол.уч | Лист | № док. | Подп. | Дата |
|---|---|---|---|---|---|
| Разраб. | | Кырпан А.С. | | | 05.10.26 |
| Пров. | | | | | |
| ГИП | | | | | |
| | | | | | |
| Н. контр. | | | | | |
| Утв. | | | | | |

**ГД-2026-003-АИ**

Трёхкомнатная квартира

Общая площадь 78,95* м² · * размеры со скана, не замерены (реестр — п. 6–11, К-13)

| Дизайн-проект интерьера трёхкомнатной квартиры | Стадия | Лист | Листов |
|---|---|---|---|
| | РП | 88 | 94 |
| **Ведомость объёмов работ (продолжение)** М 6/м | **Кырпан Александр Сергеевич** | | |

# Ведомость объёмов работ (окончание)

Объёмы по помещениям от чертежа · площади в м², длины в м · формула, правило проёмов и источник в каждой строке

## Ведомость объёмов работ по помещениям (продолжение)

| Поз. | Наименование работ (материал, число слоёв) | Ед. изм. | Объём по помещениям (№ по экспликации) | | | | | | | | Всего | Формула подсчёта | Правило проёмов | Источник | Цена за ед., ₽ | Стоимость, ₽ |
|---|---|---|---|---|---|---|---|---|---|---|---|---|---|---|---|---|
| | | | 1 | 2 | 3 | 4 | 5 | 6 | 7 | 8 | | | | | | |
| 48 | Грунтование потолка, 2 слоя | м² | 17,75 | 4,43 | 1,85 | 12,80 | 7,13 | 29,20 | 2,29 | 3,50 | 78,95 | S пом. | | л. 51 | 96 | 7 579 |
| 49 | Шпаклёвка потолка под окраску, 2 слоя, уровень Q3 | м² | 17,75 | 4,43 | 1,85 | 12,80 | 7,13 | 29,20 | 2,29 | 3,50 | 78,95 | S пом. | | л. 44, 45, 51 | 950 | 75 003 |
| 50 | Окраска потолка водно-дисперсионной краской, 2 слоя | м² | 17,75 | 4,43 | 1,85 | 12,80 | 7,13 | 29,20 | 2,29 | 3,50 | 78,95 | S пом. | | л. 51 | 360 | 28 422 |
| 51 | Окраска стен водно-дисперсионной краской, 2 слоя | м² | 44,00 | | 16,42 | 36,10 | 30,13 | 59,28 | | 23,48 | 209,41 | P × H − фартук, проёмы не вычитаются | без вычета проёмов | л. 51 | 300 | 62 823 |
| 52 | Окраска оконных откосов, 2 слоя | м.п. | 5,10 | | | 4,32 | | 8,77 | | | 18,19 | Σ (2h + b) по окнам | по окнам | л. 21 | 120 | 2 183 |
| 53 | Укладка инженерной доски на клей | м² | 17,81 | | 1,91 | 12,86 | | 29,37 | | 3,83 | 65,78 | S пом. + S в дверных проёмах | проёмы добавлены | л. 50, 51 | 1 200 | 78 936 |
| 54 | Установка плинтуса МДФ h=80 мм | м.п. | 16,80 | | 5,28 | 13,64 | 7,85 | 22,24 | | 4,53 | 70,34 | P − ширина дверных проёмов | | л. 51 | 450 | 31 653 |
| 55 | Окраска плинтуса в тоне No. 241, 2 слоя | м.п. | 16,80 | | 5,28 | 13,64 | 7,85 | 22,24 | | 4,53 | 70,34 | как плинтус | | л. 51 | 300 | 21 102 |
| 56 | Монтаж дверей скрытого монтажа под покраску (поставщик дверей) | шт | 1 | | | 1 | | 1 | | 2 | 5 | по ведомости проёмов | | л. 24 | 5 250 | 26 250 |
| 57 | Входная дверь, поставка с монтажом и откосами | шт | | | | | | | | | 1 | по ведомости проёмов | | л. 24 | по КП | |
| **Итого по разделу 3 — 608 892 ₽ (позиций 18, из них по КП 1); в сводную смету — л. 93, 94** | | | | | | | | | | | | | | | | |

## Ведомость подсчёта площадей по помещениям

| № | Помещение | S пола, м² | P, м | H, м | P × H, м² | Проёмы, м² | Стены нетто, м² | В дверных проёмах, м² | Плинтус, м | Откосы, м.п. |
|---|---|---|---|---|---|---|---|---|---|---|
| 1 | Спальня 1 | 17,75 | 17,60 | 2,50 | 44,00 | 4,83 | 39,17 | 0,06 | 16,80 | 5,10 |
| 2 | Ванная | 4,43 | 8,44 | 2,40 | 20,29 | 1,68 | 18,61 | 0,06 | нет | нет |
| 3 | Гардеробная | 1,85 | 6,08 | 2,70 | 16,42 | 1,68 | 14,74 | 0,06 | 5,28 | нет |
| 4 | Спальня 2 | 12,80 | 14,44 | 2,50 | 36,10 | 3,66 | 32,44 | 0,06 | 13,64 | 4,32 |
| 5 | Прихожая | 7,13 | 11,50 | 2,62 | 30,13 | 8,27 | 21,86 | 0,32 | 7,85 | нет |
| 6 | Кухня-гостиная | 29,20 | 24,46 | 2,50 | 61,15 | 9,59 | 51,56 | 0,17 | 22,24 | 8,77 |
| 7 | Санузел 2 | 2,29 | 6,06 | 2,40 | 14,57 | 1,47 | 13,10 | 0,05 | нет | нет |
| 8 | Коридор | 3,50 | 8,96 | 2,62 | 23,48 | 9,30 | 14,17 | 0,33 | 4,53 | нет |
| | **Итого** | **78,95** | | | **246,13** | **40,49** | **205,64** | **1,11** | **70,34** | **18,19** |

## Реестр контрольных сумм

| Показатель | По ВОР | По чертежу | Расхождение | Лист |
|---|---|---|---|---|
| Σ площадей помещений без летних, м² — общая площадь по экспликации | 78,95 | 78,95 | 0,0 % | л. 21 |
| Стены под окраску, м² (шпаклёвка) ведомость отделки | 172,07 | 172,06 | 0,0 % | л. 51 |
| Потолки под окраску, м² — ведомость отделки | 78,95 | 78,95 | 0,0 % | л. 51 |
| Плинтус, м — ведомость отделки | 70,34 | 70,34 | 0,0 % | л. 51 |
| Плитка к заказу, шт — ведомость плитки | 121 | 121 | 0,0 % | л. 46 |
| Гидроизоляция, м² — ведомость материалов плитки | 18,15 | 18,15 | 0,0 % | л. 46 |
| Точки ЭОМ, шт — планы ЭОМ (без щитов) | 130 | 132 | -1,5 % | л. 29, 30 |

## Примечания

1. Объёмы — от геометрии проекта (та же, что на планах и в ведомости отделки), не от общей площади: P — периметр чистого контура, H — от чистого пола до низа потолка, проёмы — по наружному обводу коробок.
2. Подсчёт по ГЭСН-2001-15 и ГЭСН-2001-11: штукатурка и шпаклёвка стен — за вычетом проёмов; окраска водными составами — без вычета проёмов (п. 2.24); откосы — отдельно, по ширине до 200 и более 200 мм; полы — с площадью в дверных проёмах.
3. Плитка — по раскладке (целые и с подрезкой); короб инсталляции и фартук — отдельными строками, двойного счёта облицовки нет. Материалы, запас и количество к заказу — в спецификации материалов.
4. Цены — ориентир по открытым прайсам Москвы (прайсы собраны 21.09.2026, часть расценок сверена повторно 06.10.2026), не коммерческое предложение; «по КП» — расценки нет, строка в итог не входит.
5. Демонтаж — по плану демонтажа и общим указаниям: покрытия пола, отделка стен и потолков, дверные блоки — до основания; объёмы справочные, уточняются по факту на объекте (расценки в книге нет — «по КП»).
6. Штробы в стенах — только после технического заключения о несущих стенах (общие указания, план обмера и демонтажа): строка «Штробы в стенах» вертикальные спуски кабеля от потолочной трассы к точкам, объём не меньше фактического (горизонтальные трассы — по исполнительной схеме). Расценки штробления в прайсе нет — «по КП», в итог не входит; кабель в штробах стен прокладывается после неё.
7. Площадь облицовки стен — одно число с тремя названиями: зона облицовки по ведомости отделки 31,71 м² − место за коробом инсталляции 1,68 м² (плитку туда не кладут) = стены под плитку 30,03 м² (строка «Облицовка стен»); облицовка коробов 3,23 м² — отдельной строкой; стены и короба вместе — 33,26 м² (столько плитки по раскладке в спецификации). Источник — один (quantities.js), расхождение на листах ловит.
8. Слаботочные сети: кабель по лучам от ЩС** 93,20 м (U/UTP, RG-6, домофон — по видам), гофра 83,90 м, щит ЩС** с патч-панелью; розетки RJ45 и ТВ монтируются в строке «Электроточка». Длины те же, что в ведомости изделий электрика (одна модель — low-current-engineer/bom.js); оборудование заказчика (точки доступа, камеры, коммутатор) в спецификацию не входит. 2 точ. — предложение листа слаботочки.
9. Перегородки и облицовки ГКЛ (П-1** — 2,85 м², П-2** — 1,58 м²): площадь одной стороны за вычетом проёмов, из той же модели, по которой выпущена схема каркаса; обшивка, профиль и заполнение — в спецификации материалов. П-1**, П-2** — предложение проектировщика, автором не утверждено: деньги заложены на решение, которое может измениться. Грани перегородок на ГКЛВ вычтены из штукатурки стен (7,28 м²): штукатурят основание, а не обшивку.
10. Коробы: стояков (Ш1 — 1,70 м²) и К1 над чистым полом (2,17 м открытых участков; труба К1 вдоль стен 15,72 м в короб не зашивается — она за приборами, в раме инсталляции и в шахтах). В спецификации ВК короб К1 заказывается с запасом 10 % — 2,40 м. Материалы коробов стояков и инсталляции — в спецификации материалов, К1 — в спецификации ВК.

**Допущения и предложения на листе**

Основа листа: размеры сняты со скана плана заказчика по размерным цепочкам, контрольный обмер на объекте не выполнялся (К-13); высота потолка 2700 мм принята: на плане заказчика не указана (К-11); толщины стен приняты: наружные 250 мм, перегородки 150 мм (на плане 85–190 мм) (К-13); разрешённая мощность 15 кВт принята по типовой квартире, технических условий нет (К-14); утолщение стены 190 × 1360 мм и элемент 1470 × 160 мм плана заказчика не определены (К-12); ниш санузла 2 закрыты перегородкой и фальш-стеной: проектное решение, на плане заказчика ниша у входа открыта (К-18); несущие стены не определены: до технического заключения все существующие стены считаются несущими (К-20); окна существующие и сохраняются; подоконная доска и глубина откосов не заданы — приняты, не замерены (К-27).

Знак «**» — предложение проектировщика, заказчиком не утверждено (согласовать с заказчиком): ИЗ-17: ЩС — щит слаботочный: место и состав; К-4, К-18: П-1 — проектное решение исполнителя: на плане заказчика ниша у входа открыта в кухню-гостиную; конструкция не утверждена автором (вопрос К-18), положение и размеры сняты со скана (К-13); К-18: П-2 — проектное решение исполнителя: на плане заказчика у наружной стены уступ 660 × 260 мм; конструкция не утверждена автором (вопрос К-18).

Открытые вопросы и конфликты по листу: К-28.

См. лист открытых вопросов (лист 6, записи К-4, К-11; лист 7, записи К-12–К-14, К-18, К-20; лист 8, записи К-27, К-28; лист 11, запись ИЗ-17).

| Изм. | Кол.уч | Лист | № док. | Подп. | Дата | ГД-2026-003-АИ | | | |
|---|---|---|---|---|---|---|---|---|---|
| | | | | | | Трёхкомнатная квартира | | | |
| | | | | | | Общая площадь 78,95* м² · * размеры со скана, не замерены (реестр — п. 6–11, К-13) | | | |
| Разраб. | | Кырпан А.С. | | | 05.10.26 | Дизайн-проект интерьера трёхкомнатной квартиры | Стадия | Лист | Листов |
| Пров. | | | | | | | РП | 89 | 94 |
| ГИП | | | | | | | | | |
| | | | | | | | | | |
| Н. контр. | | | | | | Ведомость объёмов работ (окончание) М 6/м | Кырпан Александр Сергеевич | | |
| Утв. | | | | | | | | | |

# Спецификация материалов

Отделочные материалы: чистое количество, запас, упаковка, к заказу · ГОСТ 21.110-2013

## Спецификация материалов (ГОСТ 21.110-2013, форма 1)

| Поз. | Наименование и техническая характеристика | Тип, марка, артикул | Код продукции | Поставщик | Ед. изм. | Количество | | | | Масса ед., кг | Примечание |
|---|---|---|---|---|---|---|---|---|---|---|---|
| | | | | | | чистое | запас, % | упаковка | к заказу | | |
| **Покрытия полов и облицовка** | | | | | | | | | | | |
| 1 | Инженерная доска (дуб натуральный, рабочий слой 4 мм, эмиссия E1, прямая укладка) | аналог: инженерная доска, дуб натуральный, масло, 1-полосная, 14/4 мм | | | м² | 65,78 | 7 | по артикулу | 70,40 м² | | пом. 1, 3, 4, 6, 8; до целой упаковки; л. 50, 51 |
| 2 | Клей для паркетной и инженерной доски (эластичный, по ТУ изготовителя доски) | по выбору подрядчика | | | м² | 65,78 | | ведро по ТУ | по ТУ | | расход кг/м² — по ТУ клея; л. 50 |
| 3 | Керамогранит 600×600 мм под травертин | аналог: керамогранит под травертин | | | шт | 24 | 10 | коробка | 27 шт | | 4 целых + 20 с подрезкой; 6,72 м² по раскладке, к заказу 9,72 м²; пом. 2, 7; л. 46–49 |
| 4 | Керамогранит 600×1200 мм под травертин | аналог: керамогранит под травертин | | | шт | 65 | 10 | коробка | 75 шт | | 16 целых + 49 с подрезкой; 33,26 м² по раскладке, к заказу 54,00 м²; пом. 2, 7; л. 46–49 |
| 5 | Керамогранит 600×1200 мм ректифицированный под травертин, матовый | аналог: керамогранит ректифицированный под травертин, матовый | | | шт | 12 | 10 | коробка | 14 шт | | 2 целых + 10 с подрезкой; 7,13 м² по раскладке, к заказу 10,08 м²; пом. 5; л. 46–49 |
| 6 | Керамогранит 1200×600 мм под травертин, матовый | аналог: керамогранит под травертин, матовый | | | шт | 4 | 10 | коробка | 5 шт | | 0 целых + 4 с подрезкой; 1,87 м² по раскладке, к заказу 3,60 м²; пом. 6; л. 46–49 |
| **Сухие смеси и гидроизоляция** | | | | | | | | | | | |
| 7 | Клей плиточный цементный класса C2 TE S1 (ГОСТ Р 56387-2018) | Ceresit CM 17 или аналог | | | кг | 349,42 | 10 | мешок 25 кг | 16 меш. | 25 | слой 5 мм, 1,50 кг/м² на 1 мм; л. 46 |
| 8 | Затирка цементная класса CG2WA, цвет — по колерной карте | Mapei Ultracolor Plus 132 или аналог | | | кг | 3,48 | 10 | упак. 2 кг | 2 упак. | 2 | расход (a+b)/ab × шов × t × 1,6 кг/м²; л. 46 |
| 9 | Гидроизоляция обмазочная полимерная, 2 слоя, лента в углах, манжеты на выводах | по выбору подрядчика | | | м² | 18,15 | 10 | ведро по ТУ | по ТУ | | пом. 2, 7; расход кг/м² — по ТУ; л. 46 |
| 10 | Лента демпферная по периметру пола из плитки | по выбору подрядчика | | | м | 20,36 | 10 | рулон | 23,00 м | | л. 46 |
| 11 | Смесь цементно-песчаная для стяжки М200 (50 мм, 33 мм) | по выбору подрядчика | | | м³ | 3,89 | 5 | мешок по ТУ | по ТУ | | S 80,06 м² × толщина; армирование и маяки — по ТУ; л. 50 |
| 12 | Смесь штукатурная гипсовая для машинного и ручного нанесения по маякам, слой до 10 мм | по выбору подрядчика | | | м³ | 198,37 | 10 | мешок по ТУ | по ТУ | | пом. 1, 2, 3, 4, 5, 6, 7, 8; расход кг/м² на 1 мм слоя — по ТУ смеси, толщина — по замеру кривизны стен; л. 21, 51 |
| **Короба из ГКЛВ** | | | | | | | | | | | |
| 13 | Лист ГКЛВ 12,5 мм, 2500 × 1200 мм, обшивка коробов в 2 слоя | по выбору подрядчика | | | м² | 9,86 | 10 | лист 3,00 м² | 4,00 лист | | инсталляция пом. 2: 1,76 м²; инсталляция пом. 7: 1,47 м²; короб Ш1 пом. 2: 1,70 м²; площадь × 2 слоя; короб К1 над полом — в спецификации ВК; л. 39, 46–49 |
| 14 | Профиль стальной оцинкованный 27 × 28 мм: каркас коробов (стойки и направляющие) | по выбору подрядчика | | | м | 24,23 | 10 | хлыст 3 м | 9 шт | | стойки через 400 мм по свободному периметру + направляющие по полу и потолку; крепёж, лента, шпаклёвка швов — по узлу короба; л. 39, 46–49 |
| **Перегородки и облицовки из ГКЛВ** | | | | | | | | | | | |
| 15 | Лист ГКЛВ 12,5 мм, 2500 × 1200 мм: обшивка перегородок и облицовок, 2 слоя на сторону | по выбору подрядчика | | | м² | 14,56 | 10 | лист 3,00 м² | 6,00 лист | | П-1**, П-2**; площадь стороны × 2 слоя × стороны (проёмы вычтены); предложение, пока П-1**, П-2** не утверждена автором (К-18, К-4); л. 22, 23, 43 |

**Допущения и предложения на листе**

Основа листа: размеры сняты со скана плана заказчика по размерным цепочкам, контрольный обмер на объекте не выполнялся (К-13); высота потолка 2700 мм принята: на плане заказчика не указана (К-11); толщины стен приняты: наружные 250 мм, перегородки 150 мм («на плане 85–190 мм) (К-13); разрешённая мощность 15 кВт принята по типовой квартире, технических условий нет (К-14); утолщение стены 190 × 1360 мм и элемент 1470 × 160 мм плана заказчика не определены (К-12); ниши санузла 2 закрыты перегородкой и фальш-стеной: проектное решение, на плане заказчика ниша у входа открыта (К-18); несущие стены не определены: до технического заключения все существующие стены считаются несущими (К-20); окна существующие и сохраняются; подоконная доска и глубина откосов не заданы — приняты, не замерены (К-27).

Знак «**» — предложение проектировщика, заказчиком не утверждено (согласовать с заказчиком): ИЗ-2, К-2, К-23: пол пом. 2, 7 — пирог пола: стяжка 33 мм и обмазочная гидроизоляция добавлены разработчиком проекта; артикул изделия не выбран: позиция описана характеристиками («аналог по характеристикам»), артикул выбирается при закупке; К-2, К-23: стены пом. 2, 7 — артикул изделия не выбран: позиция описана характеристиками («аналог по характеристикам»), артикул выбирается при закупке; К-4, К-18: П-1 — проектное решение исполнителя: на плане заказчика ниша у входа открыта в кухню-гостиную; конструкция не утверждена автором (вопрос К-18), положение и размеры сняты со скана (К-13); К-18: П-2 — проектное решение исполнителя: на плане заказчика у наружной стены уступ 660 × 260 мм; конструкция не утверждена автором (вопрос К-18); К-23: пол пом. 1, 3–6, 8, плинтус пом. 1, 3–6, 8, фартук пом. 6 — артикул изделия не выбран: позиция описана характеристиками («аналог по характеристикам»), артикул выбирается при закупке.

Открытые вопросы и конфликты по листу: К-23.

См. лист открытых вопросов (лист 6, записи К-2, К-4, К-11; лист 7, записи К-12–К-14, К-18, К-20; лист 8, записи К-23, К-27; лист 9, запись ИЗ-2).

| Изм. | Кол.уч | Лист | № док. | Подп. | Дата |
|---|---|---|---|---|---|
| Разраб. | | Кырпан А.С. | | | 05.10.26 |
| Пров. | | | | | |
| ГИП | | | | | |
| | | | | | |
| Н. контр. | | | | | |
| Утв. | | | | | |

**ГД-2026-003-АИ**

Трёхкомнатная квартира

Общая площадь 78,95* м² · * размеры со скана, не замерены (реестр — л. 6–11, К-13)

Дизайн-проект интерьера трёхкомнатной квартиры

| Стадия | Лист | Листов |
|---|---|---|
| РП | 90 | 94 |

**Спецификация материалов**

М 6/м

Кырпан Александр Сергеевич

# Спецификация материалов (продолжение)

Отделочные материалы: чистое количество, запас, упаковка, к заказу · ГОСТ 21.110-2013

## Спецификация материалов (ГОСТ 21.110-2013, форма 1) (продолжение)

| Поз. | Наименование и техническая характеристика | Тип, марка, артикул | Код продукции | Поставщик | Ед. изм. | Количество | | | | Масса ед., кг | Примечание |
|---|---|---|---|---|---|---|---|---|---|---|---|
| | | | | | | чистое | запас, % | упаковка | к заказу | | |
| 16 | Профиль направляющий ПН 100: по потолку и полу, перемычки над проёмами | по выбору подрядчика | | | м | 3,20 | 10 | хлыст 3 м | 2 шт | | П-1**, П-2**; ПН: шаг и положение стоек — на схеме каркаса; длина стойки равна высоте перегородки, стойки режут между направляющими при монтаже; предложение, пока П-1**, П-2** не утверждена автором (К-18, К-4); л. 22, 23, 43 |
| 17 | Профиль стоечный ПС 100: стойки через шаг каркаса и короткие над проёмами | по выбору подрядчика | | | м | 6,00 | 10 | хлыст 3 м | 3 шт | | П-1**, П-2**; ПС: шаг и положение стоек — на схеме каркаса; длина стойки равна высоте перегородки, стойки режут между направляющими при монтаже; предложение, пока П-1**, П-2** не утверждена автором (К-18, К-4); л. 22, 23, 43 |
| 18 | Профиль усиленный УА 100 (2,0 мм): стойки по краям проёма на полную высоту | по выбору подрядчика | | | м | 5,40 | 10 | хлыст 3 м | 2 шт | | П-1**, П-2**; УА: шаг и положение стоек — на схеме каркаса; длина стойки равна высоте перегородки, стойки режут между направляющими при монтаже; предложение, пока П-1**, П-2** не утверждена автором (К-18, К-4); л. 22, 23, 43 |
| 19 | Плита минераловатная звукопоглощающая в полость каркаса, толщина по глубине профиля 100 мм | по выбору подрядчика | | | м² | 2,85 | 10 | упаковка по ТУ | по ТУ | | П-1**, П-2**; заполнение принято (К-18): марка и плотность — при закупке; Rw системы нормируют с заполнением; предложение, пока П-1**, П-2** не утверждена автором (К-18, К-4); л. 22, 23, 43 |
| 20 | Лента уплотнительная самоклеящаяся под профили по потолку, полу и у примыканий к стенам | по выбору подрядчика | | | м | 7,90 | 10 | рулон по ТУ | 9,00 м | | П-1**, П-2**; по периметру каркаса: потолок, пол без проёма, крайние стойки у примыканий; предложение, пока П-1**, П-2** не утверждена автором (К-18, К-4); л. 22, 23, 43 |
| 21 | Саморезы для ГКЛ по металлу (по слоям обшивки), дюбели для направляющих — по ТУ изготовителя системы | по выбору подрядчика | | | м² | 14,56 | | упаковка по ТУ | по ТУ | | П-1**, П-2**; расход шт/м² и шаг дюбелей — по ТУ системы; считаются от площади обшивки; предложение, пока П-1**, П-2** не утверждена автором (К-18, К-4); л. 22, 23, 43 |
| 22 | Шпаклёвка для швов и мест креплений ГКЛВ под плитку (Q1) | по выбору подрядчика | | | м² | 4,43 | 10 | мешок по ТУ | по ТУ | | П-1**, П-2**; стороны, облицованные плиткой; сторона под окраску — в позиции шпаклёвки стен; предложение, пока П-1**, П-2** не утверждена автором (К-18, К-4); л. 22, 23, 43 |
| **Слаботочные сети** | | | | | | | | | | | |
| 23 | Кабель домофона — тип по системе поставщика | по выбору подрядчика | | | м | 2,90 | | бухта по ТУ | 3,00 м | | по лучам от ЩС**, 1 точ., запас 10 % уже в длине; 2 точ. — предложение листа слаботочки (знак «*» на плане); л. 36 |
| 24 | Кабель коаксиальный RG-6 (75 Ом) к розеткам ТВ | по выбору подрядчика | | | м | 29,10 | | бухта по ТУ | 30,00 м | | по лучам от ЩС**, 2 точ., запас 10 % уже в длине; 2 точ. — предложение листа слаботочки (знак «*» на плане); л. 36 |
| 25 | Кабель U/UTP кат. 6 (LAN, Wi-Fi и камеры по PoE) | по выбору подрядчика | | | м | 61,20 | | бухта по ТУ | 62,00 м | | по лучам от ЩС**, 5 точ., запас 10 % уже в длине; 2 точ. — предложение листа слаботочки (знак «*» на плане); л. 36 |
| 26 | Гофротруба Ø20 для слаботочных линий, отдельно от силовых | по выбору подрядчика | | | м | 83,90 | | бухта по ТУ | 84,00 м | | по длине лучей без участков в канале плинтуса (≈ 90 %); л. 36 |
| 27 | Розетка компьютерная RJ45, кат. 6, с рамкой и подрозетником | по выбору подрядчика | | | шт | 3 | | шт | 3 шт | | LAN1–LAN3; серия механизмов — как у розеток и выключателей; л. 32, 33, 36 |
| 28 | Розетка телевизионная (коаксиальная) с рамкой и подрозетником | по выбору подрядчика | | | шт | 2 | | шт | 2 шт | | ТВ1, ТВ2; серия механизмов — как у розеток и выключателей; л. 32, 33, 36 |
| 29 | Трубка или монитор домофона (поставка домофонной организации) | по выбору подрядчика | | | шт | 1 | | шт | 1 шт | | ДФ1; серия механизмов — как у розеток и выключателей; л. 32, 33, 36 |

**Допущения и предложения на листе**

Основа листа: размеры сняты со скана плана заказчика по размерным цепочкам, контрольный обмер на объекте не выполнялся (К-13); высота потолка 2700 мм принята: на плане заказчика не указана (К-11); толщины стен приняты: наружные 250 мм, перегородки 150 мм (на плане 85–190 мм) (К-13); разрешённая мощность 15 кВт принята по типовой квартире, технических условий нет (К-14); утолщение стены 190 × 1360 мм и элемент 1470 × 160 мм плана заказчика не определены (К-12); ниши санузла 2 закрыты перегородкой и фальш-стеной: проектное решение, на плане заказчика ниша у входа открыта (К-18); несущие стены не определены: до технического заключения все существующие стены считаются несущими (К-20); окна существующие и сохраняются; подоконная доска и глубина откосов не заданы — приняты, не замерены (К-27).

Знак «*» — предложение проектировщика, заказчиком не утверждено (согласовать с заказчиком): ИЗ-2, К-2, К-23: пол пом. 2, 7 — пирог пола: стяжка 33 мм и обмазочная гидроизоляция добавлены разработчиком проекта; артикул изделия не выбран: позиция описана характеристиками («аналог по характеристикам»), артикул выбирается при закупке; ИЗ-17: ЩС — щит слаботочный: место и состав; К-2, К-23: стены пом. 2, 7 — артикул изделия не выбран: позиция описана характеристиками («аналог по характеристикам»), артикул выбирается при закупке; К-4, К-18: П-1 — проектное решение исполнителя: на плане заказчика ниша у входа открыта в кухню-гостиную; конструкция не утверждена автором (вопрос К-18), положение и размеры сняты со скана (К-13); К-18: П-2 — проектное решение исполнителя: на плане заказчика у наружной стены уступ 660 × 260 мм; конструкция не утверждена автором (вопрос К-18); К-23: пол пом. 1, 3–6, 8, плинтус пом. 1, 3–6, 8, фартук пом. 6 — артикул изделия не выбран: позиция описана характеристиками («аналог по характеристикам»), артикул выбирается при закупке.

Открытые вопросы и конфликты по листу: К-23.

См. лист открытых вопросов (лист 6, записи К-2, К-4, К-11; лист 7, записи К-12–К-14, К-18, К-20; лист 8, записи К-23, К-27; лист 9, запись ИЗ-2; лист 11, запись ИЗ-17).

| Изм. | Кол.уч | Лист | № док. | Подп. | Дата |
|---|---|---|---|---|---|
| Разраб. | | Кырлан А.С. | | | 05.10.26 |
| Пров. | | | | | |
| ГИП | | | | | |
| | | | | | |
| Н. контр. | | | | | |
| Утв. | | | | | |

**ГД-2026-003-АИ**

Трёхкомнатная квартира

Общая площадь 78,95* м² · * размеры со скана, не замерены (реестр — л. 6–11, К-13)

Дизайн-проект интерьера трёхкомнатной квартиры

| Стадия | Лист | Листов |
|---|---|---|
| РП | 91 | 94 |

**Спецификация материалов (продолжение)**

М 6/м

**Кырлан Александр Сергеевич**

# Спецификация материалов (окончание)

Отделочные материалы: чистое количество, запас, упаковка, к заказу · ГОСТ 21.110-2013

## Спецификация материалов (ГОСТ 21.110-2013, форма 1) (продолжение)

| Поз. | Наименование и техническая характеристика | Тип, марка, артикул | Код продукции | Поставщик | Ед. изм. | Количество | | | | Масса ед., кг | Примечание |
|---|---|---|---|---|---|---|---|---|---|---|---|
| | | | | | | чистое | запас, % | упаковка | к заказу | | |
| 30 | Щит слаботочный ЩС**: корпус, DIN-рейка, розетки 220 В | по выбору подрядчика | | | шт | 1 | | шт | 1 шт | | ЩС**; серия механизмов — как у розеток и выключателей; л. 32, 33, 36 |
| 31 | Патч-панель, портов не менее 5 | по выбору подрядчика | | | шт | 1 | | шт | 1 шт | | серия механизмов — как у розеток и выключателей; л. 32, 33, 36 |
| **Лакокрасочные материалы** | | | | | | | | | | | |
| 32 | Краска интерьерная акриловая, матовая, класс истирания 1 | Farrow & Ball Modern Emulsion No. 30 «Hague Blue» | | | л | 9,26 | 10 | банка 2,5 л | 5 банк | | 38,58 м² × 2 сл. × 0,12 л/м²; пом. 1, 4, 6; л. 51 |
| 33 | Краска интерьерная акриловая, матовая, класс истирания 1 | Farrow & Ball Modern Emulsion No. 241 «Skimming Stone» | | | л | 28,50 | 10 | банка 2,5 л | 13 банк | | 118,75 м² × 2 сл. × 0,12 л/м²; пом. 1, 4, 5, 6, 8; л. 51 |
| 34 | Краска интерьерная акриловая, глубокоматовая, класс истирания 2 | Tikkurila Anti-Reflex 2 V503 «Winter» | | | л | 17,34 | 10 | банка 2,7 л | 8 банк | | 72,23 м² × 2 сл. × 0,12 л/м²; пом. 1 (пот.), 3 (пот.), 4 (пот.), 5 (пот.), 6 (пот.), 8 (пот.); л. 51 |
| 35 | Краска интерьерная акриловая, матовая, класс истирания 1 | Tikkurila Luja 7 V503 «Winter» | | | л | 1,61 | 10 | банка 2,7 л | 1 банк | | 6,72 м² × 2 сл. × 0,12 л/м²; пом. 2 (пот.), 7 (пот.); л. 51 |
| 36 | Краска интерьерная акриловая, матовая, класс истирания 1 | Tikkurila Harmony V503 «Winter» | | | л | 3,54 | 10 | банка 2,7 л | 2 банк | | 14,74 м² × 2 сл. × 0,12 л/м²; пом. 3; л. 51 |
| 37 | Шпаклёвка финишная полимерная под окраску (стены и потолки, Q3) | по выбору подрядчика | | | м² | 251,02 | 10 | ведро по ТУ | по ТУ | | расход кг/м² на слой — по ТУ; л. 51 |
| 38 | Грунтовка акриловая глубокого проникновения, 2 слоя | по выбору подрядчика | | | м² | 284,60 | 10 | канистра по ТУ | по ТУ | | расход л/м² — по ТУ; л. 51 |
| **Погонажные изделия и потолки** | | | | | | | | | | | |
| 39 | Плинтус напольный МДФ под покраску, h=80 мм, крепление к стене | аналог: плинтус МДФ под покраску 80×16 | | | м.п. | 70,34 | 10 | хлыст 2,4 м | 33 шт | | пом. 1, 3, 4, 5, 6, 8; длина хлыста — по артикулу; л. 51 |
| 40 | Потолок подвесной ГКЛ/ГКЛВ по каркасу Knauf П113: листы, профили, подвесы, лента, шпаклёвка швов | Knauf П113 | | | м² | 77,10 | | комплект | по л. потолков | | площадь — по ведомости потолков; число листов, профилей и подвесов — по шагам каркаса на листе потолков; л. 44, 45 |

### Примечания

1. Чистое количество — из ведомости объёмов работ и раскладки плитки; запас — отдельной графой (доска — по ведомости отделки, плитка, краска и плинтус — 10 %); «к заказу» — с запасом и кратно упаковке.
2. Плитка — штуками по раскладке, запас на каждую поверхность. Калибр (рабочий размер) и тон — одной партией на помещение, калибр указать при заказе и сверить с раскладкой до укладки.
3. Краска — 0,12 л/м² на слой (середина вилки 0,10–0,15 л/м²) по фактической площади окраски из ведомости отделки; колеровка одной партией.
4. «По ТУ» — расход задаёт производитель выбранного продукта; количество к заказу — после выбора марки.
5. Поз. 1, 3, 4, 5, 6, 39 заданы характеристиками («каналог»): марку, артикул и поставщика согласовать с заказчиком до закупки, без артикула не заказывать.
6. Штукатурная смесь — на ту же площадь, что строка ВОР «Штукатурка стен» (196,37 м²): площадь одна, расход смеси задаёт производитель.
7. Коробы инсталляции и стояков: ГКЛВ в 2 слоя и профиль 27 × 28 мм считаются по свободным граням коробов (источник — раскладка плиточника и шахты в данных); короб К1 над полом — в спецификации ВК.
8. Потолки ГКЛ: в этой спецификации — площадь системы П113; число листов, профилей и подвесов — по шагам каркаса на листе потолков (подвесы через 1000, несущие через 500, основные через 1200 мм), схема каркаса не выпущена. Сантехника, светильники и мебель — по своим спецификациям.

**Допущения и предложения на листе**

Основа листа: размеры сняты со скана плана заказчика по размерным цепочкам, контрольный обмер на объекте не выполнялся (К-13); высота потолка 2700 мм принята: на плане заказчика не указана (К-11); толщины стен приняты: наружные 250 мм, перегородки 150 мм («на плане 85–190 мм) (К-13); разрешённая мощность 15 кВт принята по типовой квартире, технических условий нет (К-14); утолщение стены 190 × 1360 мм и элемент 1470 × 160 мм плана заказчика не определены (К-12); ниши санузла 2 закрыты перегородкой и фальш-стеной: проектное решение, на плане заказчика ниша у входа открыта (К-18); несущие стены не определены: до технического заключения все существующие стены считаются несущими (К-20); окна существующие и сохраняются; подоконная доска и глубина откосов не заданы — приняты, не замерены (К-27).

Знак «*» — предложение проектировщика, заказчиком не утверждено (согласовать с заказчиком): ИЗ-2, К-2, К-23: пол пом. 2, 7 — пирог пола: стяжка 33 мм и обмазочная гидроизоляция добавлены разработчиком проекта; артикул изделия не выбран: позиция описана характеристиками («каналог по характеристикам»), артикул выбирается при закупке; ИЗ-17: ЩС — щит слаботочный: место и состав; К-2, К-23: стены пом. 2, 7 — артикул изделия не выбран: позиция описана характеристиками («каналог по характеристикам»), артикул выбирается при закупке; К-23: пол пом. 1, 3–6, 8, плинтус пом. 1, 3–6, 8, фартук пом. 6 — артикул изделия не выбран: позиция описана характеристиками («каналог по характеристикам»), артикул выбирается при закупке.

Открытые вопросы и конфликты по листу: К-23.

См. лист открытых вопросов (лист 6, записи К-2, К-11; лист 7, записи К-12–К-14, К-18, К-20; лист 8, записи К-23, К-27; лист 9, запись ИЗ-2; лист 11, запись ИЗ-17).

| | | | | | | |
|---|---|---|---|---|---|---|
| | | | | | | **ГД-2026-003-АИ** |
| | | | | | | Трёхкомнатная квартира |
| | | | | | | Общая площадь 78,95* м² · * размеры со скана, не замерены (реестр — л. 6–11, К-13) |
| Изм. | Кол.уч | Лист | № док. | Подп. | Дата | |
| Разраб. | | Кырпан А.С. | | | 05.10.26 | Дизайн-проект интерьера трёхкомнатной квартиры |
| Пров. | | | | | | Стадия: РП · Лист: 92 · Листов: 94 |
| ГИП | | | | | | |
| Н. контр. | | | | | | Спецификация материалов (окончание) · М 6/м · Кырпан Александр Сергеевич |
| Утв. | | | | | | |

# Смета ориентировочная

ПРЕДВАРИТЕЛЬНО · не для производства работ · открыто пунктов: 31 (реестр — л. 6–11)

Работы, материалы, оборудование, услуги и резерв · цены — ориентир по открытым прайсам, не коммерческое предложение

**Сводная смета (прайсы собраны 21.09.2026, часть расценок сверена повторно 06.10.2026, Москва)**

| № | Наименование работ, материалов, услуг | Ед. изм. | Кол-во | Цена за ед., ₽ | Стоимость, ₽ | | | Чей подряд | Срок поставки, дн. | Основание | Источник цены |
|---|---|---|---|---|---|---|---|---|---|---|---|
| | | | | | план | факт | разница | | | | |
| **Работы — по ведомости объёмов работ** | | | | | | | | | | | |
| 1 | Демонтаж и черновые работы (без 8 поз. по КП) | раздел | 1 | | 282 510 | | | бригада | | ВОР, поз. 1–15; л. 87–89 | по ВОР |
| 2 | Инженерные системы (без 13 поз. по КП) | раздел | 1 | | 180 881 | | | бригада | | ВОР, поз. 16–39; л. 87–89 | по ВОР |
| 3 | Чистовые работы (без 1 поз. по КП) | раздел | 1 | | 608 892 | | | бригада, поставщик | | ВОР, поз. 40–57; л. 87–89 | по ВОР |
| **Материалы — по спецификации материалов** | | | | | | | | | | | |
| 4 | Инженерная доска | м² | 70,40 | 4 513 | 317 715 | | | поставщик | | спецификация, поз. 1 | Ц7 |
| 5 | Керамогранит 600×600 мм | м² | 9,72 | 1 800 | 17 496 | | | поставщик | | спецификация, поз. 3 | Ц6 |
| 6 | Керамогранит 600×1200, 1200×600 мм | м² | 67,68 | 3 500 | 236 880 | | | поставщик | | спецификация, поз. 4, 5, 6 | Ц6 |
| 7 | Клей плиточный цементный класса C2 TE S1 | меш. | 16 | 1 800 | 28 800 | | | поставщик | | спецификация, поз. 7 | Ц7 |
| 8 | Затирка цементная класса CG2WA | упак. | 2 | 1 000 | 2 000 | | | поставщик | | спецификация, поз. 8 | Ц7 |
| 9 | Краска Farrow & Ball Modern Emulsion, банка 2,5 л | банк | 18 | 5 800 | 104 400 | | | поставщик | | спецификация, поз. 32, 33 | Ц7 |
| 10 | Краска Tikkurila (Anti-Reflex 2, Luja 7, Harmony), банка 2,7 л | банк | 11 | 3 510 | 38 610 | | | поставщик | | спецификация, поз. 34, 35, 36 | Ц6 |
| 11 | Плинтус напольный МДФ под покраску | шт | 33 | 368 | 12 144 | | | поставщик | | спецификация, поз. 39 | Ц7 |
| 12 | Прочие материалы с расходом по ТУ (клей для доски, гидроизоляция, демпферная лента, смесь для стяжки, смесь штукатурная гипсовая для машинного и ручного нанесения по маякам, лист пгп 12, профиль стальной оцинкованный 27 × 28 мм: каркас коробов (стойки и направляющие), ГКЛВ перегородок, профиль ПН, профиль ПС, профиль УА, минвата в каркас, лента уплотнительная, крепёж каркаса, шпаклёвка швов, кабель слаботочки, гофра слаботочки, изделия слаботочки, шпаклёвка, грунтовка, каркас и ГКЛ потолков) | компл | 1 | по КП | | | | поставщик | | спецификация, поз. 2, 9, 10, 11, 12, 13, 14, 15, 16, 17, 18, 19, 20, 21, 22, 23, 24, 25, 26, 27, 28, 29, 30, 31, 37, 38, 40 | |
| **Оборудование и мебель — поставка по спецификациям** | | | | | | | | | | | |
| 13 | Кухонный гарнитур по проекту кухни, изготовление и монтаж (4–8 нед.) | компл | 1 | по КП | | | | поставщик | уточн.; ориентир 4–8 нед. от замера | л. 63, 64 | |
| 14 | Двери скрытого монтажа с коробом под покраску, поставка | шт | 5 | по КП | | | | поставщик | уточн.; ориентир ≈ 30 дн. | л. 24 | |

**Допущения и предложения на листе**

Основа листа: размеры сняты со скана плана заказчика по размерным цепочкам, контрольный обмер на объекте не выполнялся (К-13); высота потолка 2700 мм принята: на плане заказчика не указана (К-11); толщины стен приняты: наружные 250 мм, перегородки 150 мм (на плане 85–190 мм) (К-13); разрешённая мощность 15 кВт принята по типовой квартире, технических условий нет (К-14); утолщение стены 190 × 1360 мм и элемент 1470 × 160 мм плана заказчика не определены (К-12); ниши санузла 2 закрыты перегородкой и фальш-стеной: проектное решение, на плане заказчика ниша у входа открыта (К-18); несущие стены не определены: до технического заключения все существующие стены считаются несущими (К-20); окна существующие и сохраняются; подоконная доска и глубина откосов не заданы — приняты, не замерены (К-27).

Открытые вопросы и конфликты по листу: К-23, К-28.

См. лист открытых вопросов (лист 6, запись К-11; лист 7, записи К-12–К-14, К-18, К-20; лист 8, записи К-23, К-27, К-28).

| Изм. | Кол.уч | Лист | № док. | Подп. | Дата |
|---|---|---|---|---|---|
| Разраб. | | Кырпан А.С. | | | 05.10.26 |
| Пров. | | | | | |
| ГИП | | | | | |
| | | | | | |
| Н. контр. | | | | | |
| Утв. | | | | | |

**ГД-2026-003-АИ**

Трёхкомнатная квартира

Общая площадь 78,95* м² · * размеры со скана, не замерены (реестр — л. 6–11, К-13)

Дизайн-проект интерьера трёхкомнатной квартиры

| Стадия | Лист | Листов |
|---|---|---|
| РП | 93 | 94 |

**Смета ориентировочная**

М 6/м

Кырпан Александр Сергеевич

# Смета ориентировочная (окончание)

ПРЕДВАРИТЕЛЬНО · не для производства работ · открыто пунктов: 31 (реестр — л. 6–11)

Работы, материалы, оборудование, услуги и резерв · цены — ориентир по открытым прайсам, не коммерческое предложение

## Сводная смета (прайсы собраны 21.09.2026, часть расценок сверена повторно 06.10.2026, Москва) (продолжение)

| № | Наименование работ, материалов, услуг | Ед. изм. | Кол-во | Цена за ед., ₽ | Стоимость, ₽ | | | Чей подряд | Срок поставки, дн. | Основание | Источник цены |
|---|---|---|---|---|---|---|---|---|---|---|---|
| | | | | | план | факт | разница | | | | |
| 15 | Оборудование заказчика слаботочных сетей: точка доступа wi-fi — 2 шт; коммутатор — 1 шт | компл | 1 | по КП | | | | заказчик | | л. 32, 33 | |
| 16 | Сантехника, светильники, мебель и предметы интерьера | компл | 1 | по КП | | | | поставщик | | л. 41; л. 42; л. 66; л. 27, 28 | |
| **Прочие работы и услуги** | | | | | | | | | | | |
| 17 | Вынос и вывоз строительного мусора | м³ | | по факту | | | | бригада | | после демонтажа | |
| 18 | Подъём материалов на этаж (лифтом или вручную — по договору) | т | | по факту | | | | бригада | | по массе поставки | |
| 19 | Доставка чистовых материалов, 10 % от поставки | | | 10 % | 75 805 | | | поставщик | | от суммы материалов | |
| 20 | Уборка после ремонта | м² | 78,95 | по факту | | | | бригада | | S квартиры | |
| | **Итого работы** | | | | **1 072 283** | | | | | | |
| | **Итого материалы** | | | | **758 045** | | | | | | |
| | **Итого прочие услуги** | | | | **75 805** | | | | | | |
| | **Резерв на непредвиденные работы и материалы, 15 %** | | | | **285 920** | | | | | | |
| | **ВСЕГО ориентировочно (без оборудования и позиций по КП)** | | | | **2 192 053** | | | | | | |

### Примечания

1. Смета ориентировочная, не коммерческое предложение: объёмы — из ведомости объёмов работ и спецификации материалов, цены — нижняя граница открытых прайсов Москвы (прайсы собраны 21.09.2026, часть расценок сверена повторно 06.10.2026); перед договором цены подтвердить у подрядчика и поставщиков.
2. Источники цен: Ц1 — Домашний мастерок: прайс на отделочные работы, 2026; Ц2 — Домашний мастерок: прайс на плиточные работы, 2026; Ц3 Домашний мастерок: прайс на электромонтажные работы, 2026; Ц4 — Профи ремонтник: штукатурно-малярные работы; Ц5 — Profi.ru: укладка керамогранита на стены, Москва 2026; Ц6 — knowledge/spec-materials.md, разд. 1 и 3: ориентир по сегментам; Ц7 — Розница Москвы, 09.2026: Леманa ПРО, KGSnab, официальный дилер Farrow & Ball.
3. Повторная сверка с прайсом: 06.10.2026 — перегородка в 2 слоя с усиленным каркасом, облицовка в 2 слоя; остальные расценки — по прайсам, собранным 21.09.2026.
4. В итог не вошли позиции «по КП» и «по факту»: оборудование и мебель, двери, материалы с расходом по ТУ, вывоз мусора, подъём и уборка.
5. В разделе 1 учтены работы по П-1** и П-2** — 9 354 ₽ (расценка Ц1 за м² конструкции; П-1** — по расценке «усиленный каркас» 2 700 ₽/м² вместо 1 500 ₽/м²: шаг стоек 400 мм или проём с обрамлением УА): это предложение проектировщика, не утверждённое автором (К-18, К-4); если конструкции не будет, строки и материалы к ним снимаются, санузел 2 пересчитывается. Обрамление проёма УА, заполнение, профиль и обшивка — материалы «по ТУ», в итог не входят.
6. Доставка — 10 % от материалов, резерв — 15 % (частный ремонт 10–20 %) отдельными строками, в количествах не спрятаны. Графы «факт» и «разница» заполняются по актам.

**Допущения и предложения на листе**

Основа листа: размеры сняты со скана плана заказчика по размерным цепочкам, контрольный обмер на объекте не выполнялся (К-13); высота потолка 2700 мм принята: на плане заказчика не указана (К-11); толщины стен приняты: наружные 250 мм, перегородки 150 мм (на плане 85–190 мм) (К-13); разрешённая мощность 15 кВт принята по типовой квартире, технических условий нет (К-14); утолщение стены 190 × 1360 мм и элемент 1470 × 160 мм плана заказчика не определены (К-12); ниши санузла 2 закрыты перегородкой и фальш-стеной: проектное решение, на плане заказчика ниша у входа открыта (К-18); несущие стены не определены: до технического заключения все существующие стены считаются несущими (К-20); окна существующие и сохраняются; подоконная доска и глубина откосов не заданы — приняты, не замерены (К-27).

Знак «**» — предложение проектировщика, заказчиком не утверждено (согласовать с заказчиком): К-4, К-18: П-1 — проектное решение исполнителя: на плане заказчика ниша у входа открыта в кухню-гостиную; конструкция не утверждена автором (вопрос К-18), положение и размеры сняты со скана (К-13); К-18: П-2 — проектное решение исполнителя: на плане заказчика у наружной стены уступ 660 × 260 мм; конструкция не утверждена автором (вопрос К-18).

Открытые вопросы и конфликты по листу: К-23, К-28.

См. лист открытых вопросов (лист 6, записи К-4, К-11; лист 7, записи К-12–К-14, К-18, К-20; лист 8, записи К-23, К-27, К-28).

| Изм. | Кол.уч | Лист | № док. | Подп. | Дата | ГД-2026-003-АИ | | | |
|---|---|---|---|---|---|---|---|---|---|
| | | | | | | Трёхкомнатная квартира | | | |
| Разраб. | | Кырпан А.С. | | | 05.10.26 | Общая площадь 78,95* м² · * размеры со скана, не замерены (реестр — п. 6–11, К-13) | | | |
| Пров. | | | | | | Дизайн-проект интерьера трёхкомнатной квартиры | Стадия | Лист | Листов |
| ГИП | | | | | | | РП | 94 | 94 |
| Н. контр. | | | | | | Смета ориентировочная (окончание) | Кырпан Александр Сергеевич | | |
| Утв. | | | | | | М б/м | | | |

11

# Визуализации

Кырлан Александр Сергеевич

выпуск 05.10.2026 № 6add39ab8d · стр. 107 из 137

# Планировочное решение · вид сверху



выпуск 05.10.2026 № 6add39ab8d · стр. 108 из 137

## Гостиная

Трёхкомнатная квартира · визуализация 2 из 30

выпуск 05.10.2026 № 6add39ab8d · стр. 109 из 137

## Гостиная · зона ТВ



выпуск 05.10.2026 № 6add39ab8d · стр. 110 из 137

## Кухня-столовая



выпуск 05.10.2026 № 6add39ab8d · стр. 111 из 137

## Спальня 1

Трёхкомнатная квартира · визуализация 5 из 30

выпуск 05.10.2026 № 6add39ab8d · стр. 112 из 137

выпуск 05.10.2026 № 6add39ab8d · стр. 113 из 137

# Спальня 2

## Прихожая

Трёхкомнатная квартира · визуализация 7 из 30

выпуск 05.10.2026 № 6add39ab8d · стр. 114 из 137

## Ванная комната



выпуск 05.10.2026 № 6add39ab8d · стр. 115 из 137

## Санузел 2



выпуск 05.10.2026 № 6add39ab8d · стр. 116 из 137

выпуск 05.10.2026 № 6add39ab8d · стр. 117 из 137

## Потолок · гостиная

## Потолок · спальня 1



выпуск 05.10.2026 № 6add39ab8d · стр. 118 из 137

## Потолок · спальня 2

Трёхкомнатная квартира · визуализация 12 из 30

выпуск 05.10.2026 № 6add39ab8d · стр. 119 из 137

## Потолок · прихожая

Трёхкомнатная квартира · визуализация 13 из 30

выпуск 05.10.2026 № 6add39ab8d · стр. 120 из 137

## Потолок · ванная



выпуск 05.10.2026 № 6add39ab8d · стр. 121 из 137

## Потолок · санузел 2



выпуск 05.10.2026 № 6add39ab8d · стр. 122 из 137

room-bath1-wB

Трёхкомнатная квартира · визуализация 16 из 30

выпуск 05.10.2026 № 6add39ab8d · стр. 123 из 137

room-bath1-wC



выпуск 05.10.2026 № 6add39ab8d · стр. 124 из 137

room-bath1-wD



выпуск 05.10.2026 № 6add39ab8d · стр. 125 из 137

room-bath2-wB



выпуск 05.10.2026 № 6add39ab8d · стр. 126 из 137

выпуск 05.10.2026 № 6add39ab8d · стр. 127 из 137

room-bath2-wC

room-bedroom1-wA

Трёхкомнатная квартира · визуализация 21 из 30

выпуск 05.10.2026 № 6add39a88d · стр. 128 из 137

room-bedroom1-wB

Трёхкомнатная квартира · визуализация 22 из 30

выпуск 05.10.2026 № 6add39ab8d · стр. 129 из 137

room-bedroom2-wA



выпуск 05.10.2026 № 6add39ab8d · стр. 130 из 137

room-bedroom2-wD



выпуск 05.10.2026 № 6add39ab8d · стр. 131 из 137

## room-corridor-wA



выпуск 05.10.2026 № 6add39ab8d · стр. 132 из 137

room-corridor-wC



выпуск 05.10.2026 № 6add39ab8d · стр. 133 из 137

room-hall-wC



выпуск 05.10.2026 № 6add39ab8d · стр. 134 из 137

room-living-wB

Трёхкомнатная квартира · визуализация 28 из 30

room-living-wC



выпуск 05.10.2026 № 6add39ab8d · стр. 136 из 137

room-living-wD

Трёхкомнатная квартира · визуализация 30 из 30

выпуск 05.10.2026 № 6add39ab8d · стр. 137 из 137