ДИЗАЙН-ПРОЕКТ ИНТЕРЬЕРА

Трёхкомнатная квартира

Warm Contemporary

78,95 м²

актуальность · комфорт · мягкая геометрия · контраст фактур · открытость · уверенность

Warm contemporary: потолки V503, стены Skimming Stone No. 241, грейж H487 в текстиле, один глубокий акцент Hague Blue No. 30 (изголовья спален, ТВ-стена).

ПАЛИТРА 60 / 30 / 10

V503	F&B No. 241	H487	F&B No. 30
60 %	60 %	30 %	10 %

АВТОР ПРОЕКТА

Кырлан Александр Сергеевич

Октябрь 2026



В1 · Вид сверху (3D): планировка с мебелью, текстилем и декором

ОБЪЕКТ	ОБЩАЯ ПЛОЩАДЬ	ПОМЕЩЕНИЙ
Трёхкомнатная квартира	78,95 м²	8, из них жилых 3
СТИЛЬ	**СТАДИЯ**	**ШИФР**
Современный (контемпорари) · warm contemporary	Рабочий проект	ГД-2026-003-АИ

					Проект: Трёхкомнатная квартира			
	Лист	№ док.	Подпись	Дата	Титульный лист	Стадия	Лист	Листов
Дизайнер	Кырлан А.С.			05.10.26		П	1	88

выпуск 05.10.2026 № 204f23b33a · стр. 1 из 88

Список листов

Лист	Наименование
1	Титульный лист
2	Список листов
3	План планировки от заказчика
4	План монтажный
5	Схема каркаса перегородки П-1
6	Кухня (пом. 6). Монтажная схема
7	Шкафы. Монтажная схема
8	Карта покрытий стен
9	Колерная карта
10	План размещения мебели и оборудования
11	Спецификация мебели и оборудования
12	Спецификация мебели и оборудования (продолжение)
13	Ведомости изделий, техники и фурнитуры
14	План выводов сантехники
15	Схема разводки водопровода и канализации
16	Спецификация сантехнического оборудования
17	Раскладка плитки. Ванная. Развёртки стен
18	Раскладка плитки. Санузел 2. Развёртки стен
19	План размещения дверей
20	План потолков
21	Разрезы и узлы потолков
22	План розеток и электровыводов
23	План слаботочных сетей
24	План освещения
25	Спецификация светильников и сценарии освещения
26	Управление светильниками
27	План вентиляции
28	План отопления
29	План покрытий пола
30	Раскладка плитки. Планы полов
31	Раскладка плитки. Прихожая. Фартук кухни
32	Визуализация. Вид сверху
33	Визуализация
34	Визуализация: Спальня 1
35	Визуализация: Спальня 1
36	Визуализация: Спальня 1
37	Развёртка стены А. Спальня 1 (пом. 1)
38	Развёртка стены Б. Спальня 1 (пом. 1)
39	Развёртка стены В. Спальня 1 (пом. 1)
40	Развёртка стены Г. Спальня 1 (пом. 1)

Лист	Наименование
41	Визуализация ванной
42	Визуализация ванной
43	Визуализация ванной
44	Визуализация ванной
45	Развёртки стен А, Б. Ванная (пом. 2)
46	Развёртка стены В. Ванная (пом. 2)
47	Развёртка стены Г. Ванная (пом. 2)
48	Развёртки стен. Гардеробная (пом. 3)
49	Визуализация: Спальня 2
50	Визуализация: Спальня 2
51	Визуализация: Спальня 2
52	Развёртка стены А. Спальня 2 (пом. 4)
53	Развёртка стены Б. Спальня 2 (пом. 4)
54	Развёртка стены В. Спальня 2 (пом. 4)
55	Развёртка стены Г. Спальня 2 (пом. 4)
56	Визуализация прихожей
57	Визуализация прихожей
58	Развёртка стены А. Прихожая (пом. 5)
59	Развёртка стены Б. Прихожая (пом. 5)
60	Развёртка стены В. Прихожая (пом. 5)
61	Развёртка стены Г. Прихожая (пом. 5)
62	Визуализация кухни-гостиной
63	Визуализация кухни-гостиной
64	Визуализация кухни-гостиной
65	Визуализация кухни-гостиной
66	Визуализация кухни-гостиной
67	Визуализация кухни-гостиной
68	Развёртка стены Б2. Кухня-гостиная (пом. 6), кухонный фронт
69	Развёртка стены В1. Кухня-гостиная (пом. 6), кухонный фронт
70	Развёртка стены А. Кухня-гостиная (пом. 6)
71	Развёртка стены Б1. Кухня-гостиная (пом. 6)
72	Развёртки стен В2, Г1. Кухня-гостиная (пом. 6)
73	Развёртка стены Г2. Кухня-гостиная (пом. 6)
74	Визуализация: Санузел 2
75	Визуализация: Санузел 2
76	Развёртки стен А, Б. Санузел 2 (пом. 7)
77	Развёртки стен В, Г. Санузел 2 (пом. 7)
78	Визуализация коридора
79	Визуализация коридора
80	Развёртки стен А, Б. Коридор (пом. 8)

Лист	Наименование
81	Развёртки стен В, Г. Коридор (пом. 8)
Д_1	Шкаф распашной М_05
Д_2	Система хранения М_07
Д_3	Шкаф-купе М_13
Д_4	Кухня (пом. 6). Развёртка гарнитура
С1	Ведомость отделки помещений
С2	Спецификация отделочных материалов
С3	Узлы


Общие указания

1. Размеры даны в мм от чистовых поверхностей стен: слой штукатурки 20 мм по блоку и 5 мм шпаклёвки по ГКЛ учтён. Перед заказом встроенной мебели — контрольный обмер после штукатурки.
2. Привязки мебели — от стен и углов помещения, а не от другой мебели.
3. Розетки, выводы и выключатели под мебель — см. лист 22 «План розеток и электровыводов»; сантехприборы и выводы воды — лист 14.
4. План расстановки не является документацией для изготовления мебели: изделия — по чертежам мебельщика; покупную мебель заменять только на изделия не больше габарита из спецификации (лист 11).
5. Встроенная мебель «стена в стену» — с зазором 10 мм с каждой стороны или с компенсаторами.
6. Развёртки — вид на стену изнутри помещения, по часовой стрелке; расположение стен на схеме листа развёртки; размеры — в мм по чистовым поверхностям; отметки — в м от ±0,000; высоты H — от чистого пола помещения до оси изделия, у декора — до центра.
7. Красные цепочки — привязки электроточек и выводов: по горизонтали от угла чистовых стен, по вертикали от чистого пола, до оси изделия; звенья короче 3 мм на листе вынесены во второй ярус (ближняя к стене цепочка).
8. У знака электроточки: марка (Р — розетка, S — выключатель, Св — светильник, ЭВ вывод кабеля), *N — число постов в рамке, гр. — группа щита, H — высота оси от чистого пола, мм; группы по клавишам выключателя — на листе выключателей.
9. Схема мебели, приборов и декора не является технической документацией для производства мебели; габариты — по паспортам изделий.
10. Марки позиций: М_NN — мебель, ОБ_NN — оборудование, С_NN — сантехника; О-N отделка (ведомость отделочных материалов, серия С).
11. Размеры мебели и изделий на заказ уточнить по месту после отделочных работ.

					Проект: Трёхкомнатная квартира
	Лист	№ док.	Подпись	Дата	
Дизайнер	Кирпич А.Ф.			05.10.26	Список листов

Стадия	Лист	Листов
П	2	88

выпуск 05.10.2026 № 204f23b33a · стр. 2 из 88

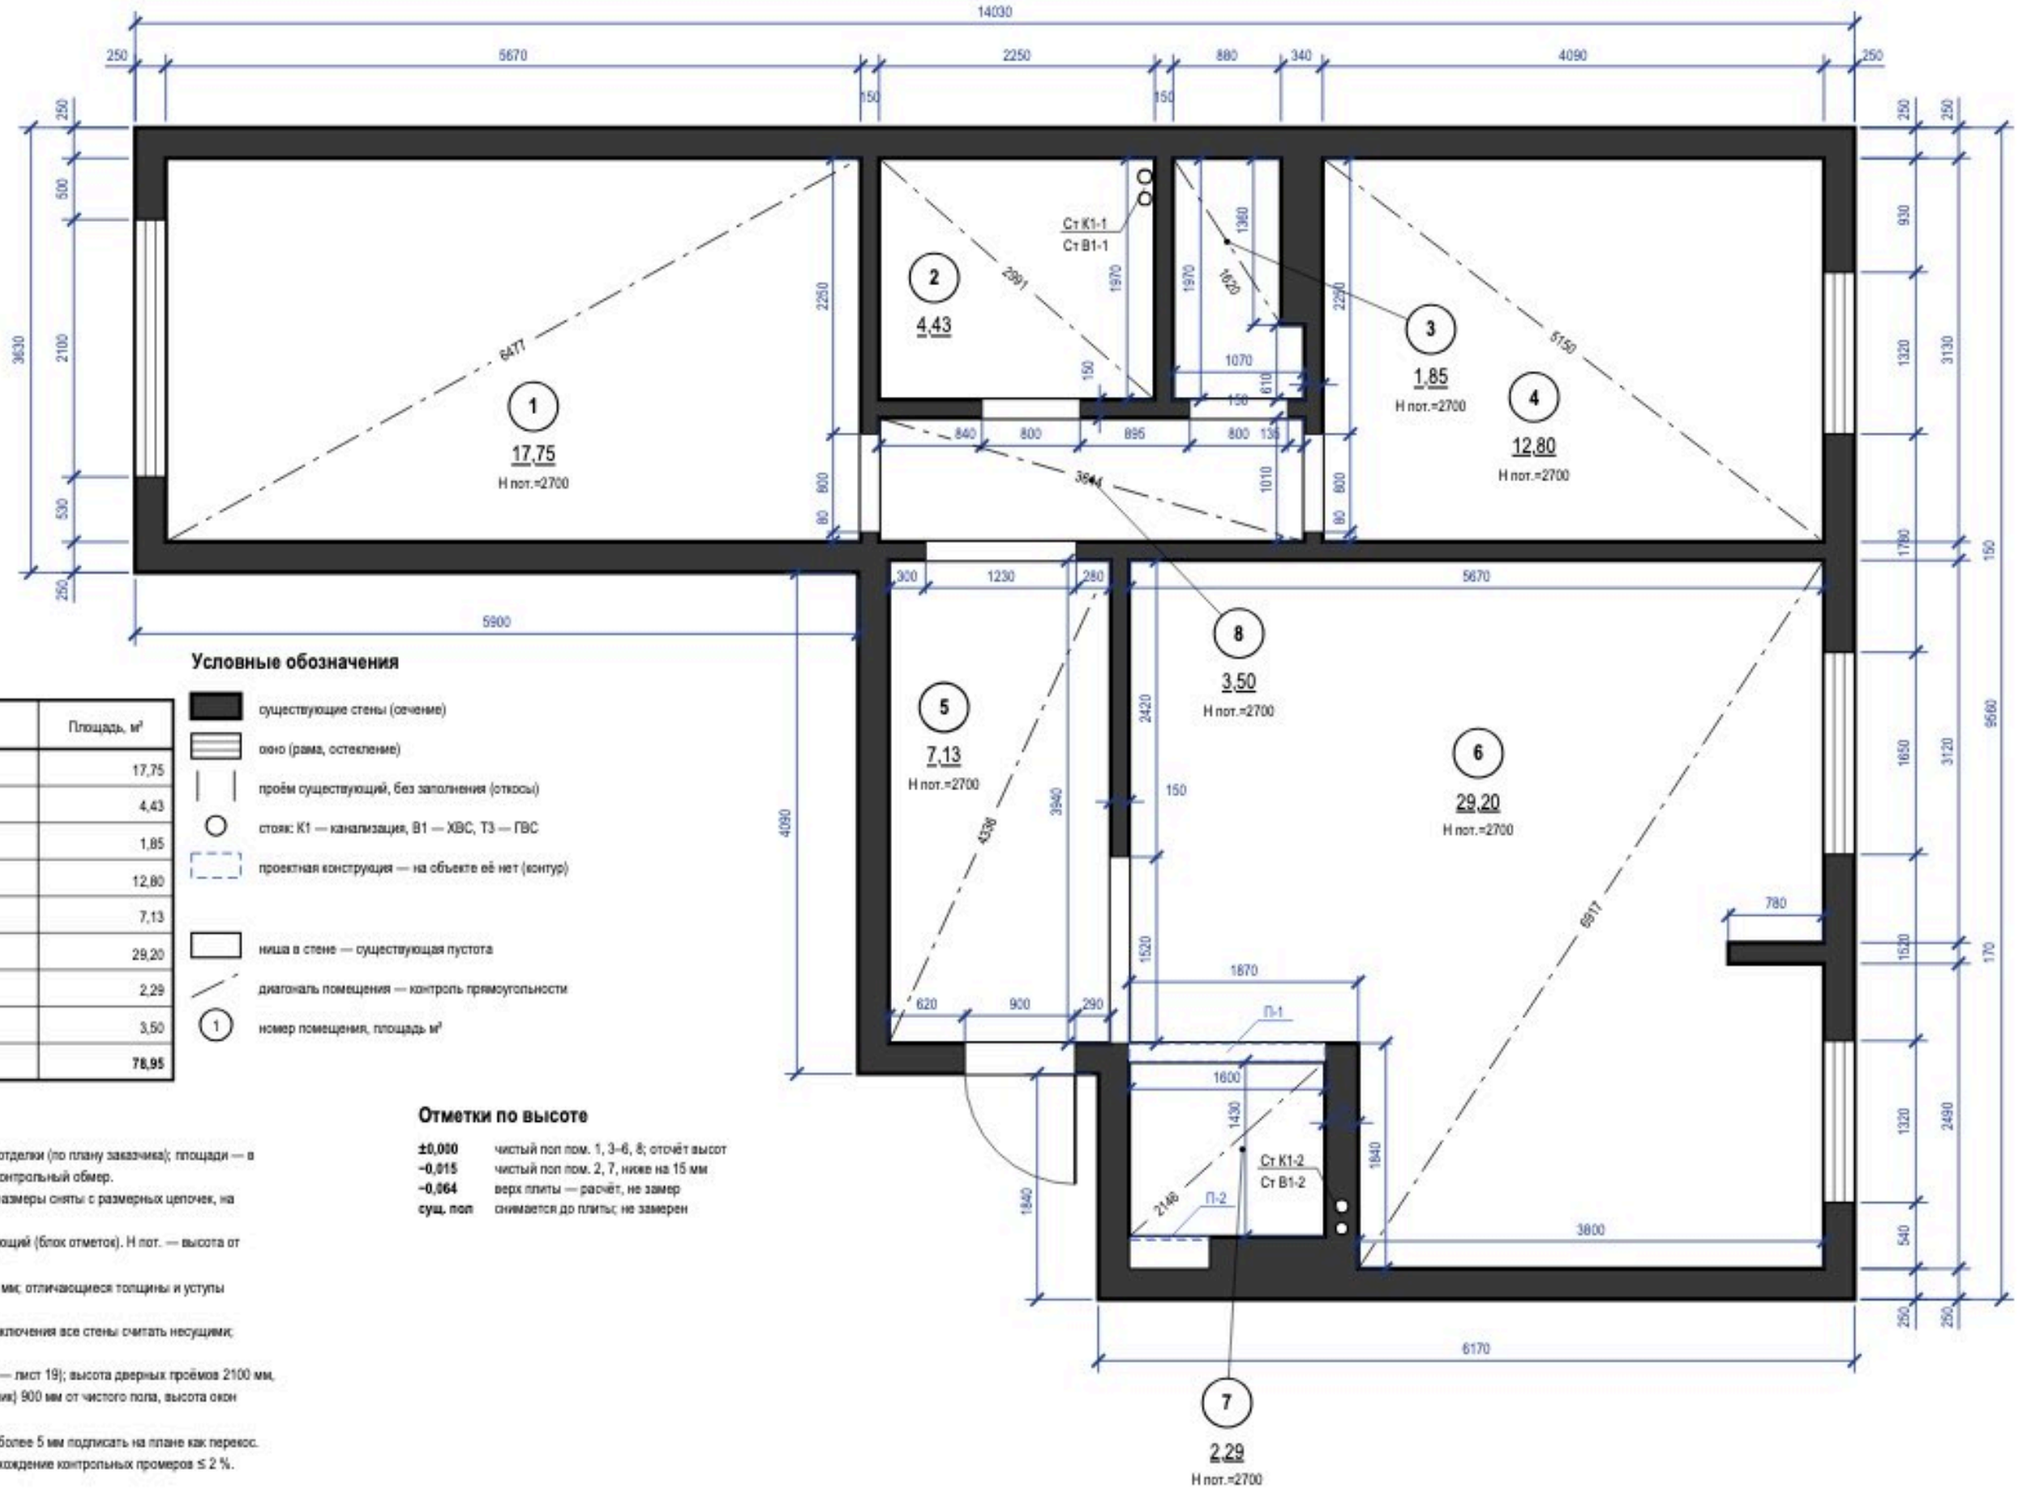

Экспликация помещений

№	Наименование	Площадь, м²
1	Спальня 1	17,75
2	Ванная	4,43
3	Гардеробная	1,85
4	Спальня 2	12,80
5	Прихожая	7,13
6	Кухня-гостиная	29,20
7	Санузел 2	2,29
8	Коридор	3,50
	Итого (общая площадь)	**78,95**

Условные обозначения

- существующие стены (сечение)
- окно (рама, остекление)
- проём существующий, без заполнения (откосы)
- стояк: К1 — канализация, В1 — ХВС, Т3 — ГВС
- проектная конструкция — на объекте её нет (контур)
- ниша в стене — существующая пустота
- диагональ помещения — контроль прямоугольности
- (1) номер помещения, площадь м²

Примечания


1. Размеры — в мм по чистым поверхностям стен до отделки (по плану заказчика); площади — в м² по тем же размерам. До начала работ выполнить контрольный обмер.
2. Источник плана: растровый скан плана заказчика, размеры сняты с размерных цепочек, на объекте не замерены.
3. За отметку ±0,000 принят чистый пол, не существующий (блок отметок). Н пот. — высота от чистого пола до плиты перекрытия.
4. Толщины стен: наружные 250 мм, перегородки 150 мм; отличающиеся толщины и уступы размерами на плане.
5. Несущие стены не определены: до технического заключения все стены считать несущими; проёмы и штробы в них не выполнять.
6. Дверные проёмы показаны без заполнения (двери — лист 19); высота дверных проёмов 2100 мм, проёмов без двери 2500, 2100 мм; низ окон (подоконник) 900 мм от чистого пола, высота окон 1500, 1400 мм.
7. Диагонали — контрольные размеры; расхождение более 5 мм подписать на плане как перекос.
8. Размеры проверить на месте до начала работ; расхождение контрольных промеров ≤ 2 %.

Отметки по высоте

±0,000	чистый пол пом. 1, 3–6, 8; отсчёт высот
−0,015	чистый пол пом. 2, 7, ниже на 15 мм
−0,064	верх плиты — расчёт, не замер
сущ. пол	снимается до плиты; не замерен

					Проект: Трёхкомнатная квартира
	Лист	№ док.	Подпись	Дата	
Дизайнер	Кырпан А.С.			05.10.26	План планировки от заказчика
					Стадия: П; Лист: 3; Листов: 88

выпуск 05.10.2026 № 204f23b33a · стр. 3 из 88

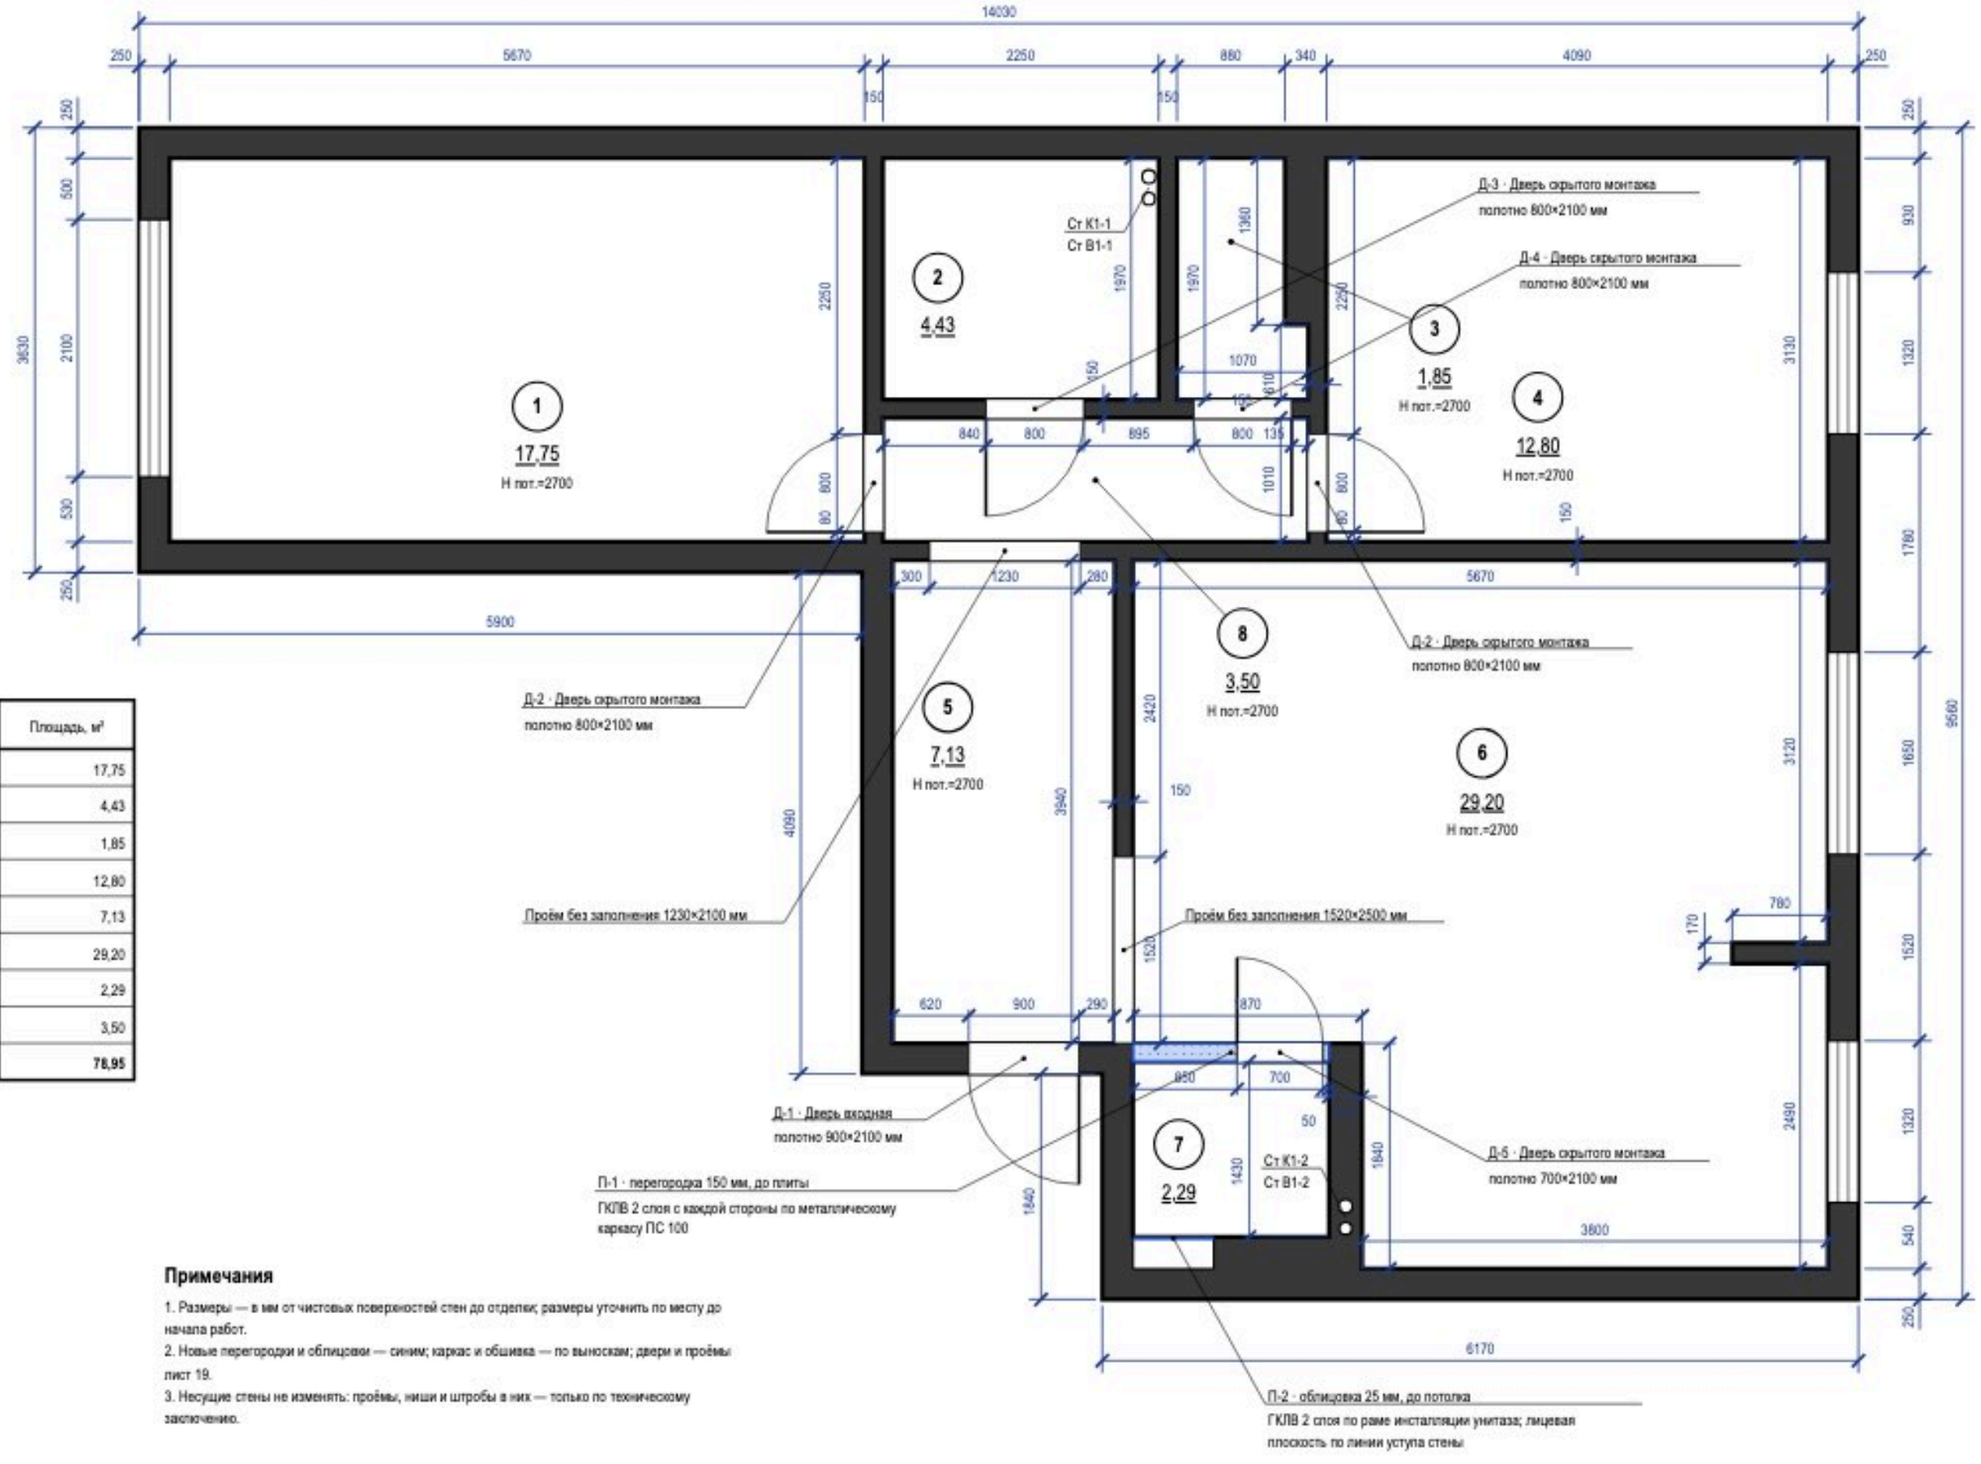

Экспликация помещений

№	Наименование	Площадь, м²
1	Спальня 1	17,75
2	Ванная	4,43
3	Гардеробная	1,85
4	Спальня 2	12,80
5	Прихожая	7,13
6	Кухня-гостиная	29,20
7	Санузел 2	2,29
8	Коридор	3,50
	Итого (общая площадь)	**78,95**

Примечания


1. Размеры — в мм от чистовых поверхностей стен до отделки; размеры уточнить по месту до начала работ.
2. Новые перегородки и облицовки — синим; каркас и обшивка — по выноскам; двери и проёмы лист 19.
3. Несущие стены не изменять: проёмы, ниши и штробы в них — только по техническому заключению.

					Проект: Трёхкомнатная квартира
	Лист	№ док.	Подпись	Дата	План монтажный
Дизайнер	Кырпан А.С.			05.10.26	

Стадия	Лист	Листов
П	4	88


выпуск 05.10.2026 № 204f23b33a · стр. 4 из 88

Вид на каркас без обшивки (М 1:20)

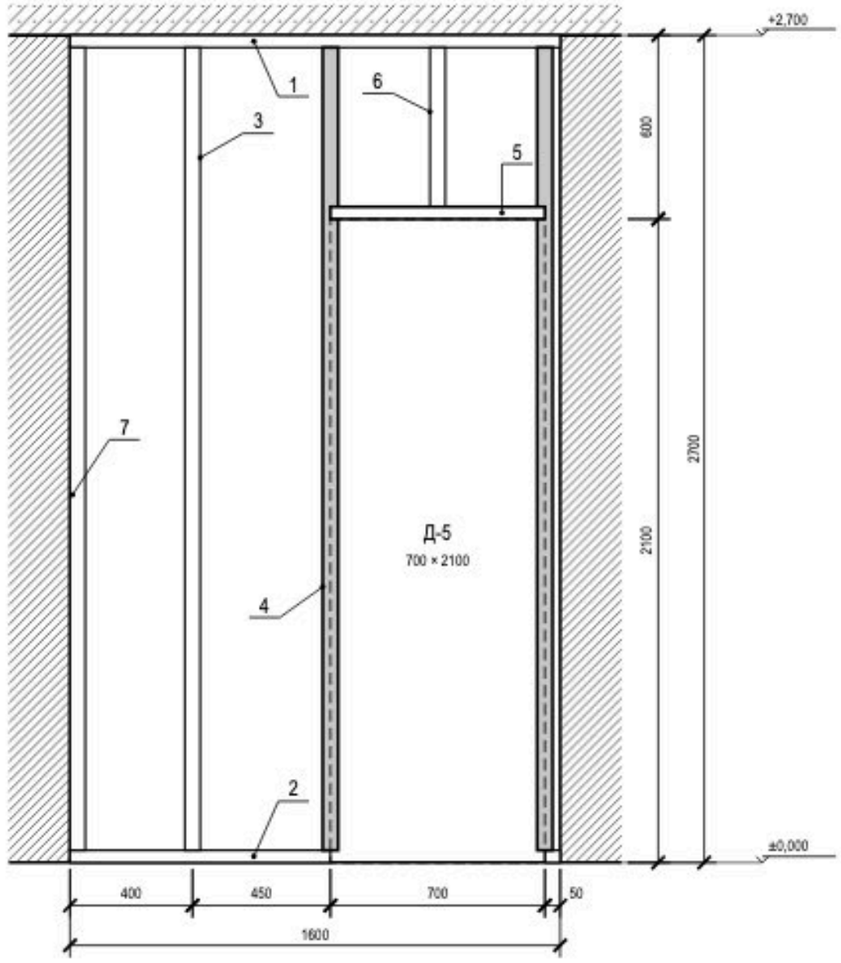


Оси — стойки каркаса; полки профиля на виде условны

Сечение А–А по стойке (М 1:5)

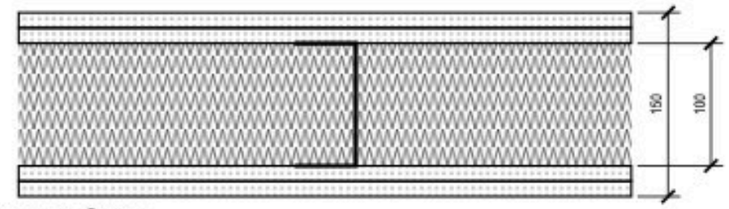


поз. 9 — ГКЛВ 12,5 мм в 2 слоя с каждой стороны; поз. 3 — ПС 100; поз. 8 — минвата 100 мм (принято)

Сечение Б–Б у проёма, на уровне ниже перемычки (М 1:5)

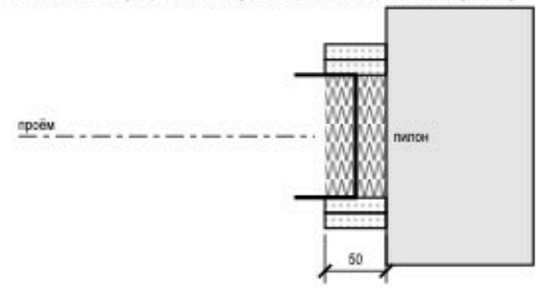


поз. 4 — УА 100, обрамление проёма; обшивка по краю проёма, простенок 50 мм до пилона

Узел 1. К плите (М 1:5)

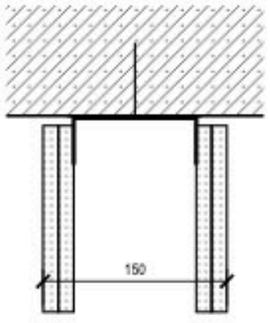

Узел 2. К полу (М 1:5)

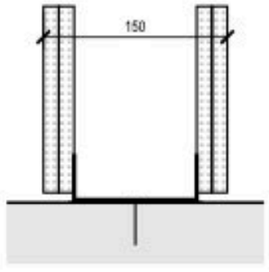

Ведомость элементов каркаса

Поз.	Наименование	Кол-во	Ед.
1	ПН 100 по потолку (по плите)	1,60	м
2	ПН 100 по полу, без проёма	0,90	м
3	ПС 100 через 400 мм	2 × 2,70	м
4	УА 100 по краям проёма	2 × 2,70	м
5	ПН 100 перемычка над проёмом	0,70	м
6	ПС 100 над перемычкой	1 × 0,60	м
7	Лента уплотнительная под профили	7,90	м
8	Минвата в полость, 100 мм	2,85	м²
9	ГКЛВ 12,5 мм, 2 слоя с двух сторон	11,40	м²

Итого: ПН 3,20 м, ПС 6,00 м, УА 5,40 м; сторона 2,85 м²

Примечания


1. П-1 (С112, ГКЛВ в 2 слоя с каждой стороны, толщина 150 мм, высота 2700 мм до плиты); ось и длина 1600 мм — со скана плана заказчика (контрольный обмер не выполнялся).
2. Шаг стоек 400 мм — по данным (под плитку и во влажной зоне). Размеры сечений профилей — «ПС 100», «УА 100» по данным и каталогу; толщины листов — ГОСТ 32614-2012.
3. Стойка ПС на 800 мм не ставится: ось в 50 мм от УА на 850 мм, два профиля с полкой 50 мм не помещаются — УА проёма служит и стойкой каркаса; полка 50 мм принята по каталогу Knauf.
4. Стойка ПС на 1600 мм не ставится: ось в 50 мм от УА на 1550 мм, два профиля с полкой 50 мм не помещаются — УА проёма служит и стойкой каркаса у конца перегородки; полка 50 мм принята по каталогу Knauf.
5. Проём Д-5 в каркасе 700 × 2100 мм принят по размеру полотна: короб скрытой двери (модель, размеры) не выбран — проём пересчитать по коробке до монтажа УА.
6. Перемычка над проёмом — направляющий профиль по верху проёма на всю его ширину; короткие стойки ПС над перемычкой на шаге каркаса: по практике узла Knauf, не по данным объекта.
7. Заполнение полости — минераловатная плита на всю глубину профиля (Rw системы С112 нормируют с заполнением); марка и плотность выбираются при закупке.
8. Длина стойки равна высоте перегородки: стойки режут на высоту между направляющими при монтаже, зазоры до плиты и пола в данных не заданы (edgeGaps).
9. Простенок 50 мм между проёмом Д-5 и концом перегородки: УА проёма — последняя стойка в 50 мм от примыкания, полоса обшивки в 50 мм уже удобной ширины; решение по положению проёма — за автором.
10. Обшивку крепят к стойкам шурупами через слой, швы слоёв разбежку; зазоры обшивки до плиты и пола, шаг дюбелей, марка заполнения — по ТУ системы и узлу изготовителя.

					Проект: Трёхкомнатная квартира
	Лист	№ док.	Подпись	Дата	
Дизайнер	Кырпан А.С.			05.10.26	Схема каркаса перегородки П-1


Стадия	Лист	Листов
П	5	88

выпуск 05.10.2026 № 204f23b33a · стр. 5 из 88

Привязка выводов и крепление модулей

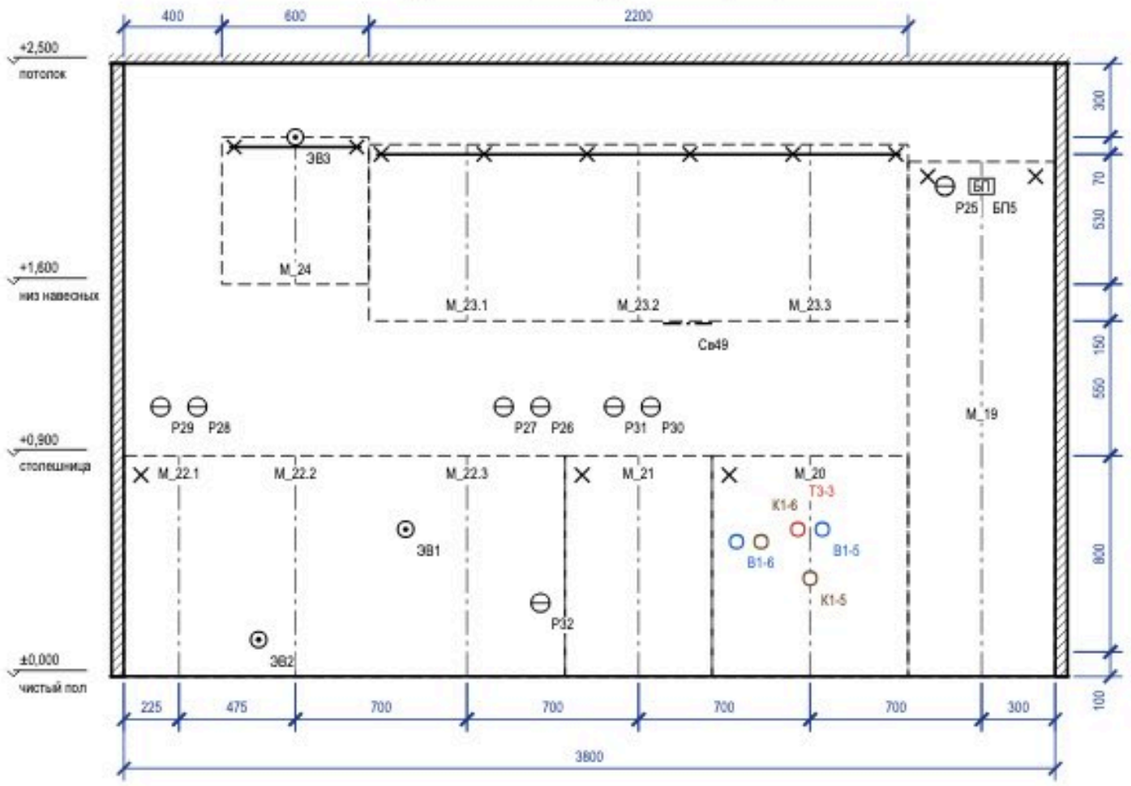

План столешницы

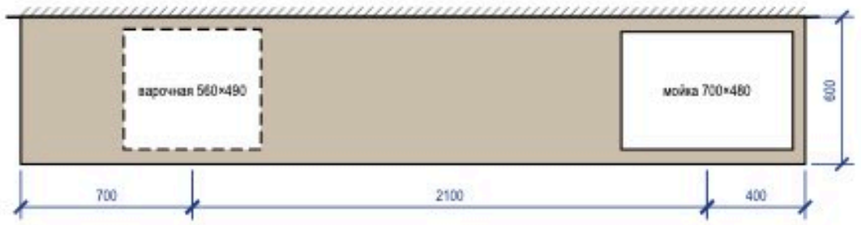

Примечания

1. Выводы — по проекту электрики и ВК; привязка по горизонтали — от оси модуля (плюс — вправо по виду), по высоте — от чистого пола до оси вывода.
2. Пенал — уголки к стене 2 шт. сверху; нижние модули — стяжками между собой и уголком к стене; ряд выставить по уровню опорами цоколя.
3. Розетки над столешницей — не ниже 150 мм над ней и не за корпусом техники; розетка за ПММ, духовым шкафом и холодильником — только в соседнем модуле или в зоне цоколя с доступом.
4. Столешница — вырезы по шаблонам выбранных моделей мойки и варочной панели; торцы у стены — герметик, пристеночный плинтус.

Привязка выводов к осям модулей

Код	Назначение	Модуль	От оси, мм	H, мм	Размещение
Р29	розетка — фартук	M_22.1	−75	1100	над столешницей (фартук)
Р28	розетка ×2 — фартук	M_22.1	+75	1100	над столешницей (фартук)
ЭВ2	вывод кабеля — духовой шкаф	M_22.2	−150	150	под духовым шкафом, доступ через ящик
ЭВ3	вывод кабеля — вытяжка	M_24	0	2200	в навесном модуле
ЭВ1	вывод кабеля — варочная панель (в соседнем модуле M_22.3, за ящиком)	M_22.3	−250	600	в соседнем модуле, за ящиком
Р27	розетка — фартук	M_22.3	+150	1100	над столешницей (фартук)
Р26	розетка ×2 — фартук	M_22.3	+300	1100	над столешницей (фартук)
Р32	розетка — посудомоечная машина	M_22.3	+300	300	в соседнем модуле, за ящиком
Р31	розетка — фартук между мойкой и варочной	M_21	−100	1100	над столешницей (фартук)
Р30	розетка ×2 — фартук между мойкой и варочной	M_21	+50	1100	над столешницей (фартук)
Св49	светодиодная лента — подсветка столешницы	M_21	+200	1440	в профиле по низу навесного модуля
В1-6	В1 — кран ПММ в шкафу мойки	M_20	−300	550	в модуле мойки
К1-6	К1 Ø40 — слив ПММ в шкафу мойки	M_20	−200	550	в модуле мойки
Т3-3	Т3 — межос. 100	M_20	−50	600	в модуле мойки
К1-5	К1 Ø50 — мойка	M_20	0	400	в модуле мойки
В1-5	В1 — межос. 100	M_20	+50	600	в модуле мойки
Р25	розетка — холодильник, над нишей M_19 (съёмная панель)	M_19	−150	2000	над нишей холодильника, съёмная панель
БП5	блок питания — в пенале M_19, верх, съёмная панель	M_19	0	2000	над нишей холодильника, съёмная панель

Зазоры под отделку

Поверхность	Отделка	Зазор, мм	Учесть
фартук	керамогранит	10	от чернового основания до корпуса навесных и столешницы
стены	окраска	5	под штукатурку и шпаклёвку за пеналом
пол	инженерная доска		цоколь — после укладки пола, опоры ±20 мм

Условные обозначения

- навесной модуль (невидимый контур)
- ось модуля (от неё — привязка вывода)
- анкер / уголок крепления к стене
- розетка на стене
- вывод кабеля к технике
- В1 — вывод воды В1 / Т3, канализации К1

	Лист	№ док.	Подпись	Дата
Дизайнер	Кырпан А.С.			05.10.26


Проект: Трёхкомнатная квартира

Кухня (пом. 6). Монтажная схема


Стадия	Лист	Листов
П	6	88

выпуск 05.10.2026 № 204f23b33a · стр. 6 из 88


Шкаф распашной M_05 (пом. 1)

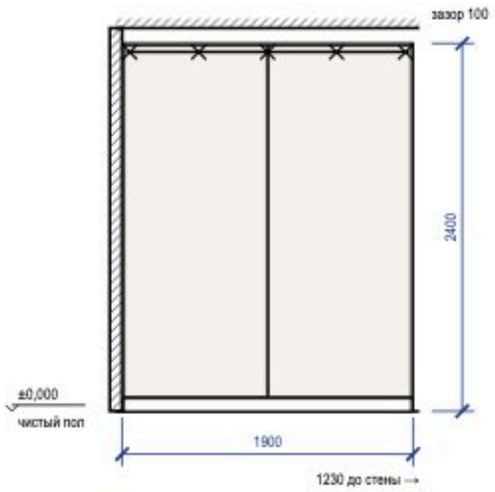

Система хранения M_07 (пом. 3)

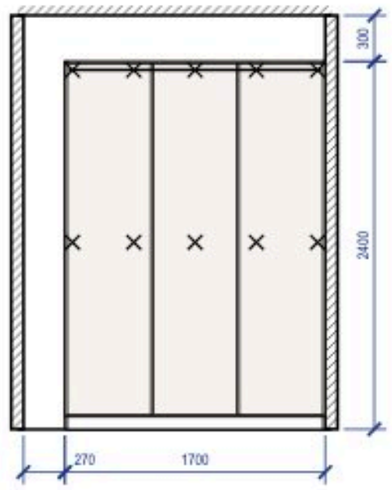

Шкаф-купе M_13 (пом. 5)

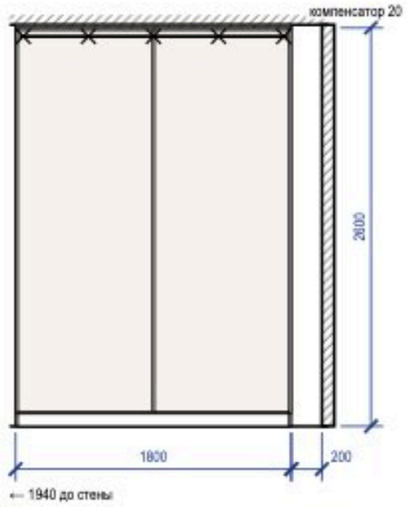

Крепление и зазоры под отделку

Марка	Помещение, стена	Основание	Отделка стены	Зазор, мм	Крепёж по плане	От опрокидывания
M_05	Спальня 1 (1), стена Б	по основанию — см. таблицу крепежа	окраска	5	анкер 5 шт., шаг 450	уголок к стене, 2 шт.
M_07	Гардеробная (3), стена Г	по основанию — см. таблицу крепежа	окраска	5	анкер 10 шт. (2 ряда)	крепление к стене, 3 точки
M_13	Прихожая (5), стена Г	по основанию — см. таблицу крепежа	окраска	5	анкер 5 шт., шаг 425	уголки 2 шт.

Крепёж по основанию стены

Основание стены	Крепёж
бетон, ж/б	анкер-шуруп 7,5×72 или дюбель 8×60 с шурупом 5×70
кирпич полнотелый	дюбель 8×80 с шурупом 5×90
газобетон, пазогребень	дюбель для газобетона 10×100 или химический анкер
гипсокартон	закладная до обшивки (брус 40×80 или фанера 18 мм), саморез в закладную

Условные обозначения


- × — анкер / уголок крепления к стене
- ▭ — корпус и полки ЛДСП (вид на стену)
- ▨ — компенсатор — короб до потолка

Примечания

1. Установочные размеры — от чистого пола и чистых стен; перед установкой контрольный замер после отделки.
2. Порядок: корпус выставить по уровню опорами цоколя → закрепить к стене по задней планке → навесить двери и фасады, отрегулировать зазоры → подогнать и закрепить компенсатор.
3. Анкеры — с шагом не более 500 мм, не ближе 50 мм от края планки; на ГКЛ только в закладную, установленную до обшивки.
4. Скрытые коммуникации под анкеры проверить детектором; трассы электрики по плану розеток.
5. Сборка стоя на месте: M_13 (диагональ боковины 2668 мм > 2620 мм до потолка) — корпус не собирается лёжа и не поднимается собранным, а собирается в проектном положении у стены; выставление по уровню и крепление к стене выполняются по корпусу, собранному на месте.

					Проект: Трёхкомнатная квартира	
	Лист	№ док.	Подпись	Дата	Шкафы. Монтажная схема	Стадия / Лист / Листов
Дизайнер	Кырпан А.С.			05.10.26		П / 7 / 88

выпуск 05.10.2026 № 204f23b33a · стр. 7 из 88

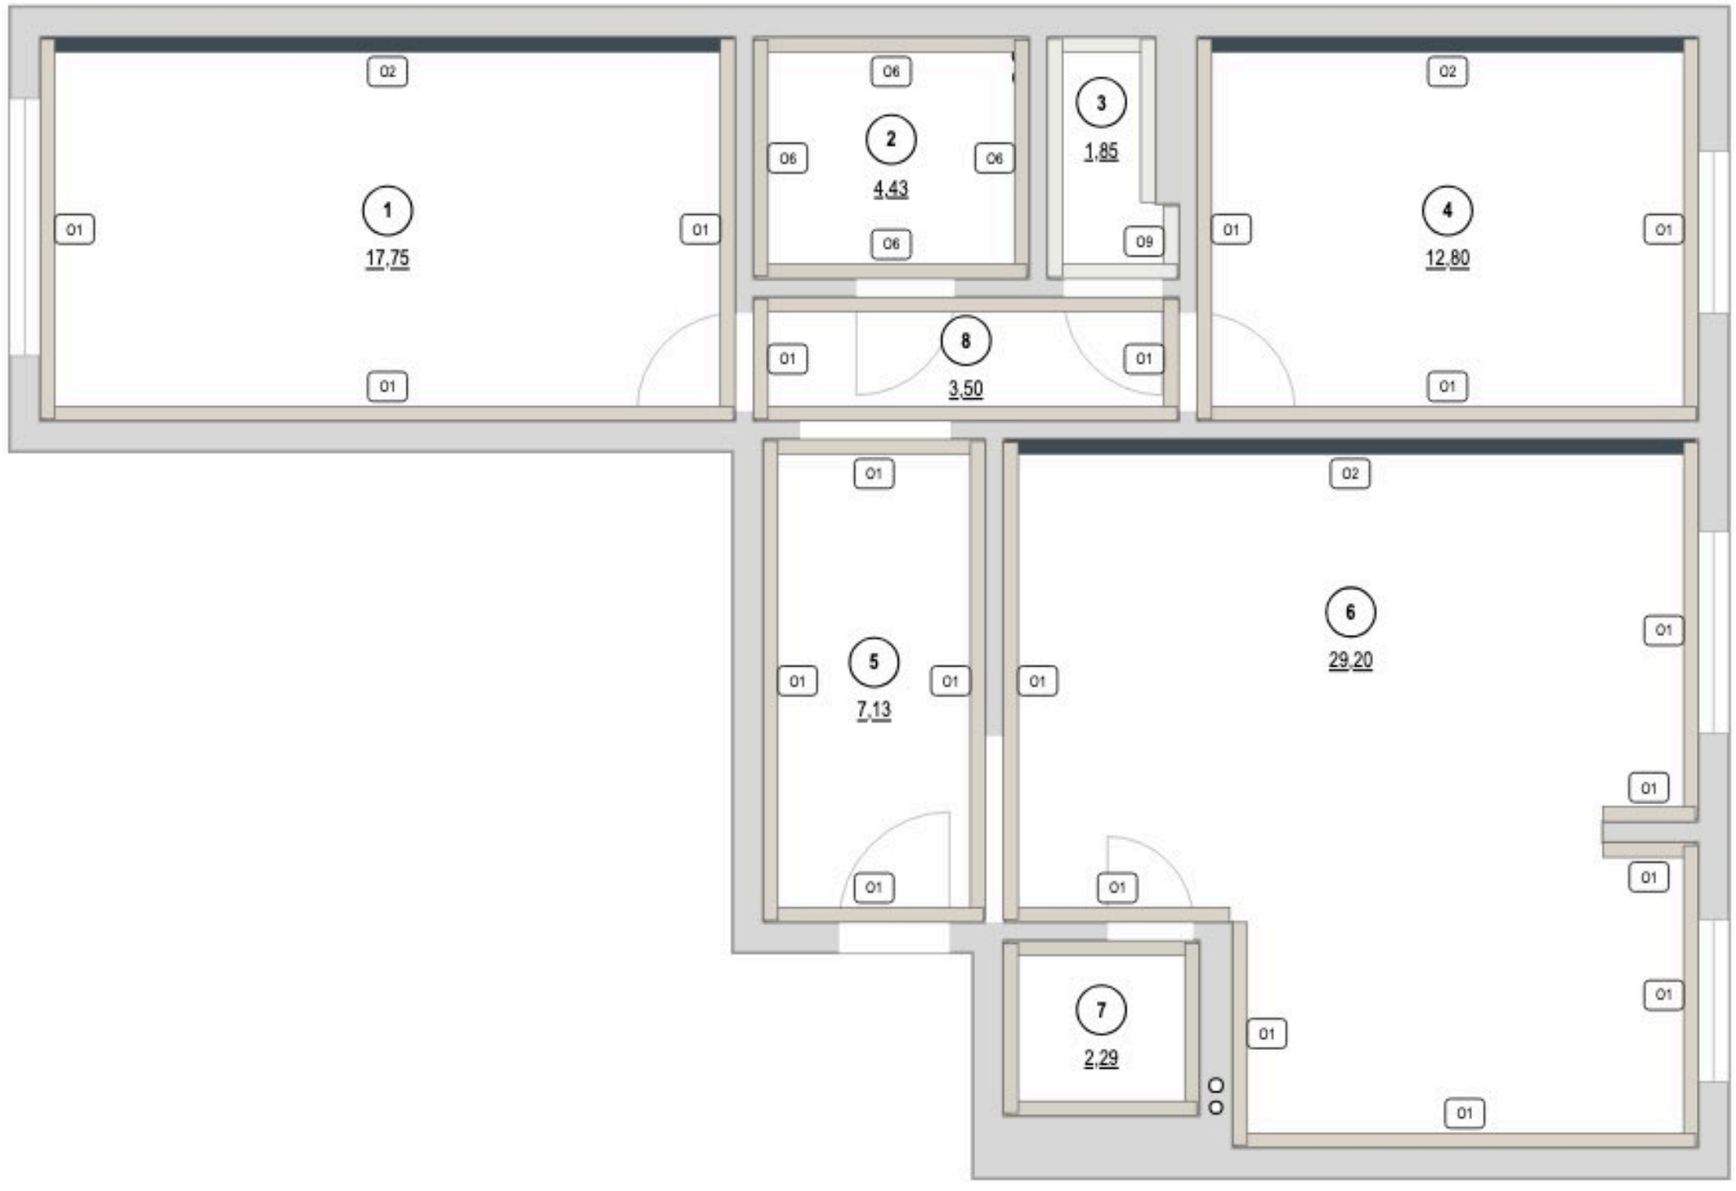

Покрытия стен

Марка	Покрытие	Помещение: S, м²	Итого, м²
O1	окраска Farrow & Ball · No. 241 «Skimming Stone»	1: 24,8; 4: 22,0; 5: 21,6; 6: 34,2; 8: 13,9	116,4
O2	окраска Farrow & Ball · No. 30 «Hague Blue»	1: 14,1; 4: 10,2; 6: 14,1	38,3
O6	облицовка плиткой · 600×1200 мм	2: 18,1; 7: 12,6	30,8
O9	окраска Tikkurila · V503 «Winter»	3: 13,8	13,8

Площади — нетто, по развёрткам (за вычетом проёмов и фартука); высоты помещений — от чистого пола.

					Проект: Трёхкомнатная квартира			
	Лист	№ док.	Подпись	Дата	Карта покрытий стен	Стадия	Лист	Листов
Дизайнер	Кырпан А.С.			05.10.26		П	8	88

выпуск 05.10.2026 · 204f23b33a · стр. 8 из 88

Колерная карта по помещениям

Помещение	Поверхность	Образец	Поз.	Система и код цвета	Производитель, линейка / материал, артикул	Блеск	Класс EN 13300	LRV	Площадь
1. Спальня 1 17,75 м²	стены		K1	Farrow & Ball No. 241	Farrow & Ball · Modern Emulsion	матовая	1	67	25,0 м²
	акцент А		K2	Farrow & Ball No. 30	Farrow & Ball · Modern Emulsion	матовая	1	7	14,2 м²
	потолок		K3	Tikkurila V503	Tikkurila · Anti-Reflex 2	глубокомат.	2	86	17,8 м²
	пол		KM1	по образцу	инженерная доска · аналог по хар.				17,8 м²
	плинтус		K4	Farrow & Ball No. 241	МДФ · в цвет Farrow & Ball			67	16,8 м
2. Ванная 4,43 м²	стены		KM2	по образцу	плитка · аналог по хар.				18,6 м²
	потолок		K5	Tikkurila V503	Tikkurila · Luja 7	матовая	1	86	4,4 м²
	пол		KM3	по образцу	керамогранит · аналог по хар.				4,4 м²
3. Гардеробная 1,85 м²	стены		K6	Tikkurila V503	Tikkurila · Harmony	матовая	1	86	14,7 м²
	потолок		K3	Tikkurila V503	Tikkurila · Anti-Reflex 2	глубокомат.	2	86	1,9 м²
	пол		KM1	по образцу	инженерная доска · аналог по хар.				1,9 м²
	плинтус		K7	Tikkurila V503	МДФ · в цвет Tikkurila			86	5,3 м
4. Спальня 2 12,8 м²	стены		K1	Farrow & Ball No. 241	Farrow & Ball · Modern Emulsion	матовая	1	67	22,2 м²
	акцент А		K2	Farrow & Ball No. 30	Farrow & Ball · Modern Emulsion	матовая	1	7	10,2 м²
	потолок		K3	Tikkurila V503	Tikkurila · Anti-Reflex 2	глубокомат.	2	86	12,8 м²
	пол		KM1	по образцу	инженерная доска · аналог по хар.				12,8 м²
	плинтус		K4	Farrow & Ball No. 241	МДФ · в цвет Farrow & Ball			67	13,6 м
5. Прихожая 7,13 м²	стены		K1	Farrow & Ball No. 241	Farrow & Ball · Modern Emulsion	матовая	1	67	21,9 м²
	потолок		K3	Tikkurila V503	Tikkurila · Anti-Reflex 2	глубокомат.	2	86	7,1 м²
	пол		KM4	по образцу	керамогранит · аналог по хар.				7,1 м²
	плинтус		K4	Farrow & Ball No. 241	МДФ · в цвет Farrow & Ball			67	7,8 м
6. Кухня-гостиная 29,2 м²	стены		K1	Farrow & Ball No. 241	Farrow & Ball · Modern Emulsion	матовая	1	67	35,5 м²
	акцент А		K2	Farrow & Ball No. 30	Farrow & Ball · Modern Emulsion	матовая	1	7	14,2 м²
	потолок		K3	Tikkurila V503	Tikkurila · Anti-Reflex 2	глубокомат.	2	86	29,2 м²
	пол		KM1	по образцу	инженерная доска · аналог по хар.				29,2 м²
	плинтус		K4	Farrow & Ball No. 241	МДФ · в цвет Farrow & Ball			67	22,2 м
	фартук		KM5	по образцу	керамогранит · аналог по хар.				1,9 м²
7. Санузел 2 2,29 м²	стены		KM2	по образцу	плитка · аналог по хар.				13,1 м²
	потолок		K5	Tikkurila V503	Tikkurila · Luja 7	матовая	1	86	2,3 м²
	пол		KM3	по образцу	керамогранит · аналог по хар.				2,3 м²
8. Коридор 3,5 м²	стены		K1	Farrow & Ball No. 241	Farrow & Ball · Modern Emulsion	матовая	1	67	14,2 м²
	потолок		K3	Tikkurila V503	Tikkurila · Anti-Reflex 2	глубокомат.	2	86	3,5 м²
	пол		KM1	по образцу	инженерная доска · аналог по хар.				3,5 м²
	плинтус		K4	Farrow & Ball No. 241	МДФ · в цвет Farrow & Ball			67	4,5 м

Перечень выкрасов на согласование

№	Код	Бренд / веер	Пом. / стена	Подложка	Формат	Статус
1	No. 241	Farrow & Ball	1, 4, 5, 6, 8	ГКЛ, загрунтованный под эту краску; МДФ, загрунтованный под эмаль	600×1000; 300×600	к выполнению
2	No. 30	Farrow & Ball	1 А, 4 А, 6 А	ГКЛ, загрунтованный под эту краску	600×1000	к выполнению
3	V503	Tikkurila	1, 2, 3, 4, 5, 6, 7, 8	ГКЛ, загрунтованный под эту краску; МДФ, загрунтованный под эмаль	600×1000; 300×600	к выполнению

Примечания

1. Цвет утверждается только по выкрасу на объекте: формат от А3 до 1000×1000 мм на загрунтованном ГКЛ, в 2 слоя (как на стене), не на белой шпаклёвке; смотреть днём и при свете проекта своего помещения, рядом с образцами пола и фасадов. Подпись на обороте: код, бренд и веер, дата.
2. Колеровка машинная в колеровочном центре бренда; каждый код — за один проход, одной партией на весь объём. Колеровщику передаётся только система и код утверждённого веера; плашки и HEX на листе — ориентир, печать не является эталоном цвета.
3. Класс мокрого истирания — EN 13300 (ISO 11998); блеск — по ГОСТ 31975 (ISO 2813), геометрия 60°. LRV — пересчёт координаты L каталога производителя ($Y = ((L^*+16)/116)^3$); «≈» — расчёт по HEX, справочно.
4. Площади поверхностей — тем же способом и с теми же цифрами, что в ведомости отделки (способ счёта — в общих указаниях); объём краски к заказу, фасовка и материалы КМ — в спецификации отделочных материалов.
5. Перечень выкрасов составлен по кодам колерной карты; к основному тону стен добавить на выкрас 2 соседних тона того же веера (светлее и темнее), статус отмечать в графе «Статус» при согласовании.

Схема квартиры: цвет стен и акценты (б/м)

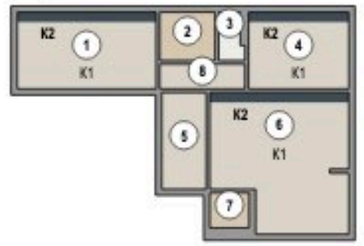


Схема палитры проекта

Стиль: Современный (контемпорари) · схема: аналоговая

основной	основной	второстепенный	акцентный
Tikkurila V503	**Farrow & Ball No. 241**	**Tikkurila H487**	**Farrow & Ball No. 30**
Winter LRV 86 потолок 1,2,3,4,5,6,7,8; стены 3; плинтус 3; текстиль/декор 1,4,6	Skimming Stone LRV 67 стены 1,4,5,6,8; плинтус 1,4,5,6,8	Pumice LRV 57 текстиль/декор 1,4,6	Hague Blue LRV 7 акцент 1,4,6; текстиль/декор 1,4,6

План 60/30/10

60%	30%	10%

Окраска, факт — по площади стен, акцентов, потолков

85%	15%

окрашено всего 251 м²; второстепенный тон несут мебель и текстиль

Текстиль и декор в цветах вне палитры проекта

- NCS S 3005-Y20R тёплый тауп-серый — пом. 1 (Т3)
- Farrow & Ball No. 229 Elephant's Breath — пом. 4 (Т10)
- Tikkurila V484 Driftwood — пом. 4 (Т9), 6 (Т15, Т16, Т19)
- Farrow & Ball No. 47 Green Smoke — пом. 4 (Т11)


Условные обозначения

- **K1** Farrow & Ball No. 241 · Skimming Stone · Modern Emulsion · матовая · кл. 1
- **K2** Farrow & Ball No. 30 · Hague Blue · Modern Emulsion · матовая · кл. 1
- **K3** Tikkurila V503 · Winter · Anti-Reflex 2 · глубокомат. · кл. 2
- **K4** Farrow & Ball No. 241 · Skimming Stone · МДФ
- **K5** Tikkurila V503 · Winter · Luja 7 · матовая · кл. 1
- **K6** Tikkurila V503 · Winter · Harmony · матовая · кл. 1
- **K7** Tikkurila V503 · Winter · МДФ
- дерево (доска, паркет, ламинат) — рисунок досок
- керамогранит, плитка, камень — сетка швов по формату
- **KM1** аналог: инженерная доска, дуб натуральный, масло, 1-полосная, 14/4 мм
- **KM2** плитка · аналог: керамогранит под травертин, матовый, 600×1200×9 мм
- **KM3** аналог: керамогранит ректифицированный под травертин, матовый, 600×600×9 мм
- **KM4** аналог: керамогранит ректифицированный под травертин, матовый, 600×1200×9 мм
- **KM5** аналог: керамогранит под травертин, матовый, 1200×600×9 мм

K — позиция окраски (код + продукт + блеск), КМ — позиция материала, тон КМ — по описанию артикула, эталон — образец материала; ≈ LRV — расчёт по HEX, справочно

					Проект: Трёхкомнатная квартира			
	Лист	№ док.	Подпись	Дата	Колерная карта	Стадия	Лист	Листов
Дизайнер	Кырпан А.С.			05.10.26		П	9	88

выпуск 05.10.2026 № 204f23b33a · стр. 9 из 88

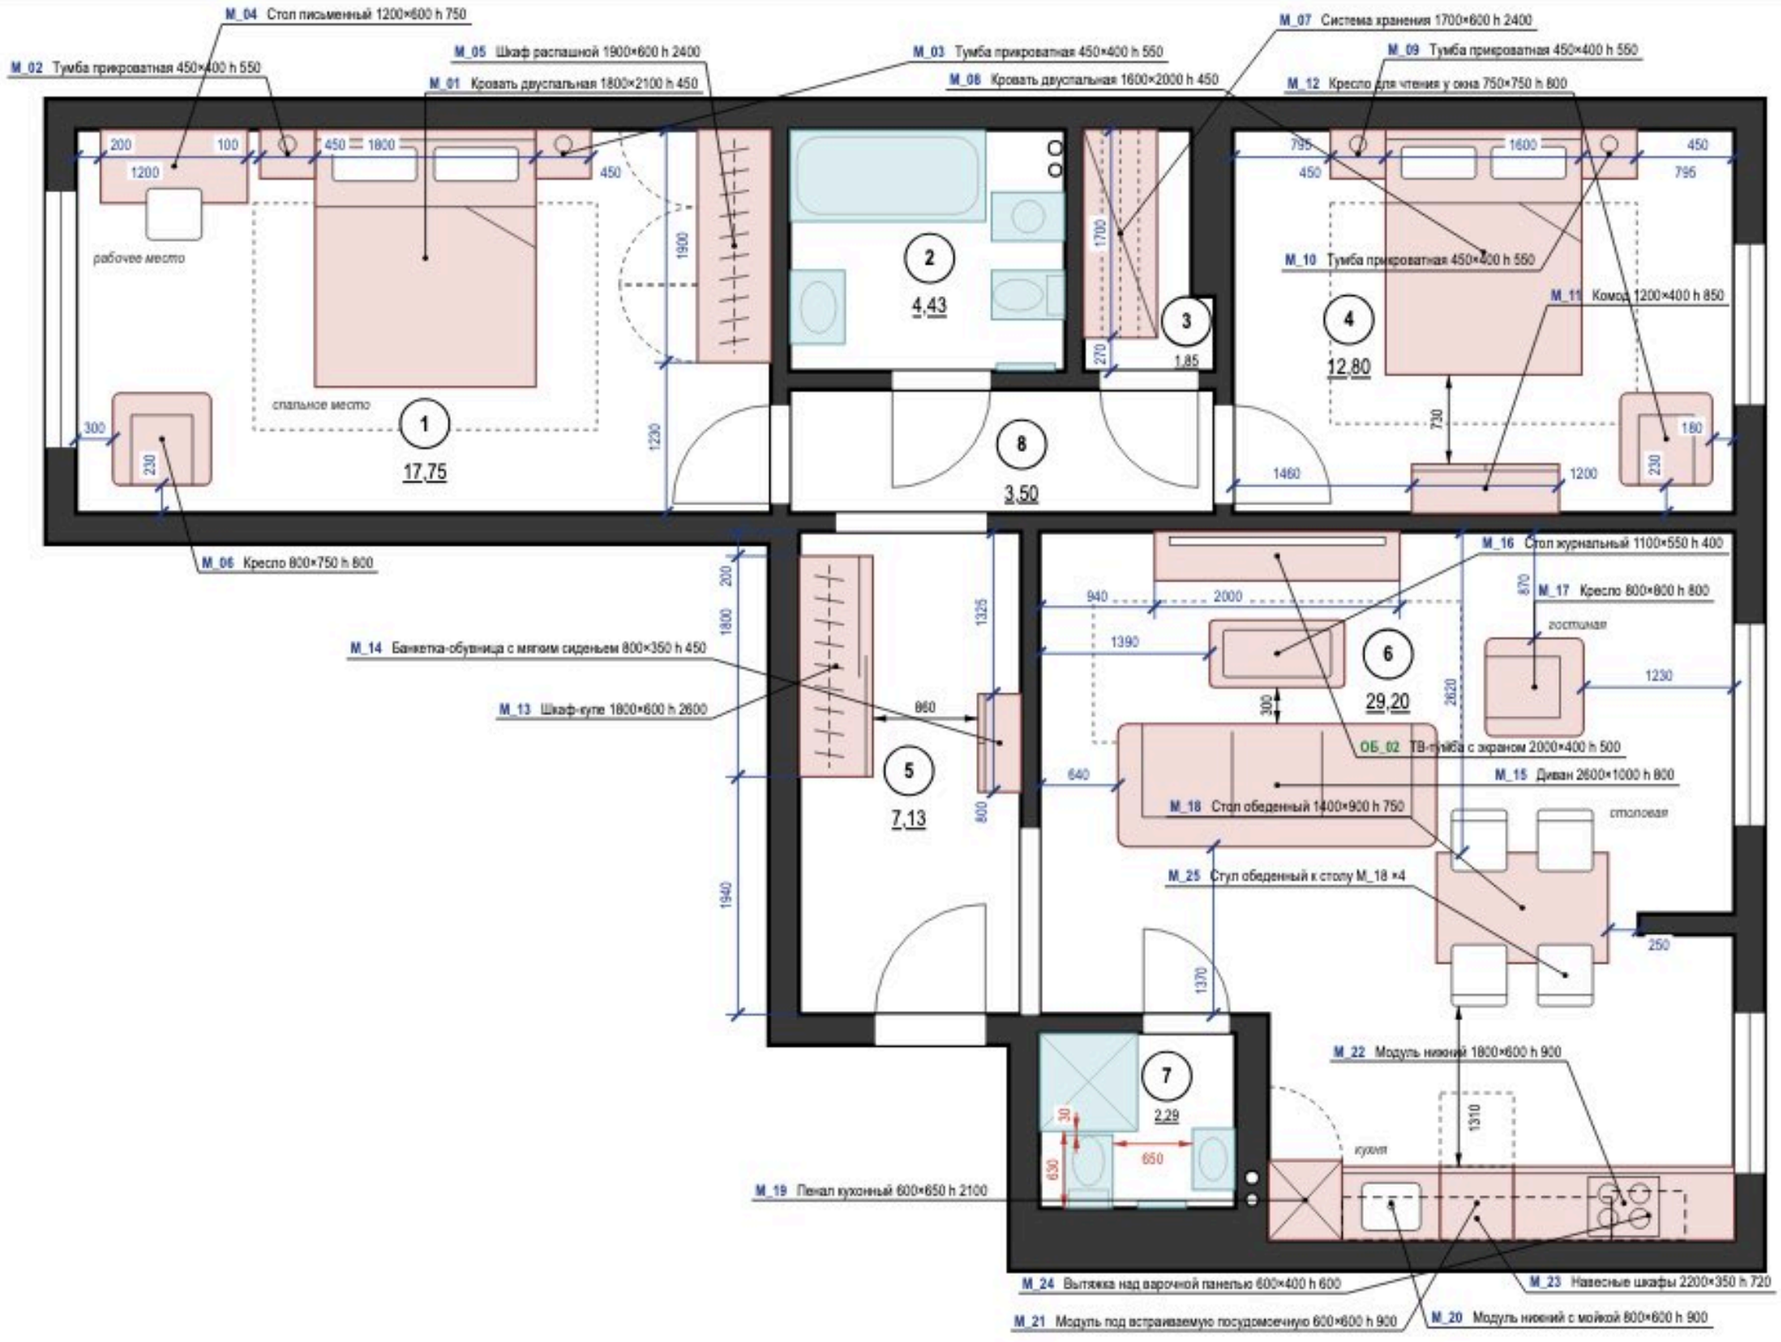

Экспликация помещений

лист обмерного плана · на плане — номера в марках

Ведомость мебели и оборудования

Марка	Наименование	Ш×Г×В, мм	Пом.	Кол.
M_01	Кровать двуспальная	1800×2100×450	1	1
M_02	Тумба прикроватная	450×400×550	1	1
M_03	Тумба прикроватная	450×400×550	1	1
M_04	Стол письменный	1200×600×750	1	1
M_05	Шкаф распашной	1900×600×2400	1	1
M_06	Кресло	800×750×800	1	1
M_07	Система хранения	1700×600×2400	3	1
M_08	Кровать двуспальная	1600×2000×450	4	1
M_09	Тумба прикроватная	450×400×550	4	1
M_10	Тумба прикроватная	450×400×550	4	1
M_11	Комод	1200×400×850	4	1
M_12	Кресло для чтения у окна	750×750×800	4	1
M_13	Шкаф-купе	1800×600×2600	5	1
M_14	Банкетка-обувница с мягким сиденьем	800×350×450	5	1
ОБ_02	ТВ-тумба с экраном	2000×400×500	6	1
M_15	Диван	2600×1000×800	6	1
M_16	Стол журнальный	1100×550×400	6	1
M_17	Кресло	800×800×800	6	1
M_18	Стол обеденный	1400×900×750	6	1
M_19	Пенал кухонный	600×650×2100	6	1
M_20	Модуль нижний с мойкой	800×600×900	6	1
M_21	Модуль под встраиваемую посудомоечную	600×600×900	6	1
M_22	Модуль нижний	1800×600×900	6	1
M_23	Навесные шкафы	2200×350×720	6	1
M_24	Вытяжка над варочной панелью	600×400×600	6	1
M_25	Стул обеденный к столу M_18	450×500×820	6	4

Ш — вдоль стены (изголовья), Г — от стены (длина кровати)

Материалы, модели, допуск замены — лист 11

Примечания

1. Размеры — в мм от чистовых поверхностей стен; размеры мебели уточнить после отделочных работ; общие указания — лист 2.
2. Стулья обеденной группы (M_25 — 4 шт.) показаны в рабочем положении, задвинутыми под столешницу на 150 мм.

					Проект: Трёхкомнатная квартира
	Лист	№ док.	Подпись	Дата	План размещения мебели и оборудования
Дизайнер	Кырпан А.С.			05.10.26	

Стадия	Лист	Листов
П	10	88

выпуск 05.10.2026 № 204f23b33a · стр. 10 из 88

Поз.	Наименование и техническая характеристика	Тип, марка, обозначение документа, опросного листа	Код продукции	Поставщик	Ед. измерения	Кол.	Масса 1 ед., кг	Примечание
	Мебель встроенная и корпусная (изготовление по чертежам мебельщика)							
M_05	Шкаф распашной; корпус ЛДСП, фасады — матовая эмаль в цвет стен (Farrow & Ball No. 241); Ш×Г×В 1900×600×2400 мм			изготовление на заказ	шт.	1		пом. 1; крепление к стене
M_07	Система хранения: штанги, полки, ящики; каркас и полки — ЛДСП, декор «дуб натуральный»; Ш×Г×В 1700×600×2400 мм			изготовление на заказ	шт.	1		пом. 3; крепление к стене
M_13	Шкаф-купе; корпус ЛДСП, фасады — матовая эмаль в цвет стен (Farrow & Ball No. 241); Ш×Г×В 1800×600×2600 мм			изготовление на заказ	шт.	1		пом. 5
M_19	Пенал кухонный, холодильник; корпус ЛДСП, фасады — матовая эмаль в тон стен; Ш×Г×В 600×650×2100 мм			изготовление на заказ	шт.	1		пом. 6; крепление к стене
M_20	Модуль нижний с мойкой; корпус ЛДСП, фасады — матовая эмаль в тон стен; Ш×Г×В 800×600×900 мм			изготовление на заказ	шт.	1		пом. 6
M_21	Модуль под встраиваемую посудомоечную машину; корпус ЛДСП, фасады — матовая эмаль в тон стен; Ш×Г×В 600×600×900 мм			изготовление на заказ	шт.	1		пом. 6
M_22	Модуль нижний: ящики, варочная панель, духовой шкаф, бутылочница; корпус ЛДСП, фасады — матовая эмаль в тон стен; Ш×Г×В 1800×600×900 мм			изготовление на заказ	шт.	1		пом. 6
M_23	Навесные шкафы, 3 секции; корпус ЛДСП, фасады — матовая эмаль в тон стен; Ш×Г×В 2200×350×720 мм			изготовление на заказ	шт.	1		пом. 6
M_24	Вытяжка над варочной панелью; корпус ЛДСП, фасады — матовая эмаль в тон стен; Ш×Г×В 600×400×600 мм			изготовление на заказ	шт.	1		пом. 6
	Мебель покупная							
M_01	Кровать двуспальная; мягкое изголовье, обивка — ткань, цвет Tikkurila H487; Ш×Г×В 1800×2100×450 мм			аналог по характеристикам	шт.	1		пом. 1; замена ≤ габарита
M_02, M_03, M_09, M_10	Тумба прикроватная; шпон, дуб натуральный, матовое масло; Ш×Г×В 450×400×550 мм			аналог по характеристикам	шт.	4		пом. 1, 4; замена ≤ габарита
M_04	Стол письменный; шпон, дуб натуральный, матовое масло; Ш×Г×В 1200×600×750 мм			аналог по характеристикам	шт.	1		пом. 1; замена ≤ габарита
M_06	Кресло; обивка — ткань, цвет Tikkurila H487; Ш×Г×В 800×750×800 мм			аналог по характеристикам	шт.	1		пом. 1; замена ≤ габарита
M_08	Кровать двуспальная; мягкое изголовье, обивка — ткань, цвет Tikkurila H487; Ш×Г×В 1600×2000×450 мм			аналог по характеристикам	шт.	1		пом. 4; замена ≤ габарита
M_11	Комод; шпон, дуб натуральный, матовое масло; Ш×Г×В 1200×400×850 мм			аналог по характеристикам	шт.	1		пом. 4; крепление к стене; замена ≤ габарита
M_12	Кресло для чтения у окна; обивка — ткань, цвет Tikkurila H487; Ш×Г×В 750×750×800 мм			аналог по характеристикам	шт.	1		пом. 4; замена ≤ габарита
M_14	Банкетка-обувница с мягким сиденьем, над ней настенная вешалка с полкой (низ 1650); шпон, дуб натуральный, матовое масло; Ш×Г×В 800×350×450 мм			аналог по характеристикам	шт.	1		пом. 5; замена ≤ габарита
M_15	Диван; обивка — ткань, цвет Tikkurila H487; Ш×Г×В 2600×1000×800 мм			аналог по характеристикам	шт.	1		пом. 6; замена ≤ габарита
M_16	Стол журнальный; шпон, дуб натуральный, матовое масло; Ш×Г×В 1100×550×400 мм			аналог по характеристикам	шт.	1		пом. 6; замена ≤ габарита
M_17	Кресло; обивка — ткань, цвет Tikkurila H487; Ш×Г×В 800×800×800 мм			аналог по характеристикам	шт.	1		пом. 6; замена ≤ габарита
M_18	Стол обеденный; шпон, дуб натуральный, матовое масло; Ш×Г×В 1400×900×750 мм			аналог по характеристикам	шт.	1		пом. 6; замена ≤ габарита
M_25	Стул обеденный к столу M_18; обивка — ткань, цвет Tikkurila H487; каркас — дуб натуральный; Ш×Г×В 450×500×820 мм			аналог по характеристикам	шт.	4		пом. 6; замена ≤ габарита
ОБ_02	ТВ-тумба с экраном; шпон, дуб натуральный, матовое масло; Ш×Г×В 2000×400×500 мм			аналог по характеристикам	шт.	1		пом. 6; замена ≤ габарита
	Техника встраиваемая и бытовая, светильники под розетки							
	Стиральная машина, место по листу ВК (ОБ_01); Ш×Г 600×400 мм			аналог по характеристикам	шт.	1		пом. 2; по схеме изготовителя
	Холодильник встраиваемый, в модуле M_19			аналог по характеристикам	шт.	1		пом. 6; по схеме изготовителя
	Посудомоечная машина встраиваемая, в модуле M_21; ниша 600 мм			аналог по характеристикам	шт.	1		пом. 6; по схеме изготовителя
	Варочная панель встраиваемая, электрическая, в модуле M_22			аналог по характеристикам	шт.	1		пом. 6; по схеме изготовителя
	Духовой шкаф встраиваемый, в модуле M_22			аналог по характеристикам	шт.	1		пом. 6; по схеме изготовителя
	Вытяжка, в модуле M_24			аналог по характеристикам	шт.	1		пом. 6; по схеме изготовителя

Примечания

1. Позиции мебели совпадают с марками на плане расстановки; размеры Ш×Г×В — Ш вдоль стены, Г от стены.
2. Встроенная и корпусная мебель изготавливается по чертежам мебельщика после контрольного обмера; графы «Тип, марка» и «Код продукции» для неё не заполняются (ГОСТ 21.110-2013).
3. Покупные изделия — аналог по характеристикам: заменять только на изделия не больше указанного габарита и того же материала и цвета.
4. Материал и цвет, не указанные в данных изделия, приняты по концепции: тон дерева — по полу, обивка — по вторичному цвету палитры; образцы согласовать до заказа.
5. Масса 1 ед. для изделий до 25 кг не указывается. Техника — по монтажным схемам изготовителя; выводы — по листам ЭОМ и ВК.

					Проект: Трёхкомнатная квартира
	Лист	№ док.	Подпись	Дата	Спецификация мебели и оборудования
Дизайнер	Кырпан А.С.			05.10.26	

Стадия	Лист	Листов
П	11	88

Поз.	Наименование и техническая характеристика	Тип, марка, обозначение документа, опросного листа	Код продукции	Поставщик	Ед. измерения	Кол.	Масса 1 ед., кг	Примечание
	Торшер, у поз. M_06; абажур — ткань или опаловое стекло; лампа 2700 K			аналог по характеристикам	шт.	1		пом. 1; розетка P5 (ЭОМ)
	Торшер, у поз. ОБ_02; абажур — ткань или опаловое стекло; лампа 2700 K			аналог по характеристикам	шт.	1		пом. 6; розетка P21 (ЭОМ)
	Текстиль							
Т1	Портьеры-волна; лён 100 %; цвет Tikkurila H487; карниз 2500 мм, высота 2610 мм, сборка 2			аналог по характеристикам	шт.	2		пом. 1
Т2	Тюль; полиэстер 100 %; цвет Tikkurila V503; карниз 2500 мм, высота 2610 мм, сборка 2,5			аналог по характеристикам	шт.	1		пом. 1
Т3	Ковёр под кроватью; шерсть 80 %, хлопок 20 %; цвет NCS S 3005-Y20R; 2800×1850 мм			аналог по характеристикам	шт.	1		пом. 1; с подложкой
Т4	Подушки декоративные на кровать; лён 100 %; цвет Tikkurila H487			аналог по характеристикам	шт.	3		пом. 1
Т5	Подушки на кровать, акцент; хлопковый бархат 100 %; цвет Farrow & Ball No. 30			аналог по характеристикам	шт.	2		пом. 1
Т6	Плед на кровать; шерсть меринос 100 %; цвет Farrow & Ball No. 30			аналог по характеристикам	шт.	1		пом. 1
Т7	Портьеры-волна; лён 100 %; цвет Tikkurila H487; карниз 1820 мм, высота 2610 мм, сборка 2			аналог по характеристикам	шт.	2		пом. 4
Т8	Тюль; полиэстер 100 %; цвет Tikkurila V503; карниз 1820 мм, высота 2610 мм, сборка 2,5			аналог по характеристикам	шт.	1		пом. 4
Т9	Ковёр под кроватью; шерсть 100 %; цвет Tikkurila V484; 2500×1800 мм			аналог по характеристикам	шт.	1		пом. 4; с подложкой
Т10	Подушки декоративные на кровать; букле (шерсть 60 %, полиэстер 40 %); цвет Farrow & Ball No. 229			аналог по характеристикам	шт.	3		пом. 4
Т11	Подушки на кровать, акцент; хлопковый бархат 100 %; цвет Farrow & Ball No. 47			аналог по характеристикам	шт.	2		пом. 4
Т12	Плед на кровать; шерсть меринос 100 %; цвет Farrow & Ball No. 30			аналог по характеристикам	шт.	1		пом. 4
Т13	Портьеры-волна (гостиная); лён 70 %, вискоза 30 %; цвет Tikkurila H487; карниз 2250 мм, высота 2610 мм, сборка 2			аналог по характеристикам	шт.	2		пом. 6
Т14	Тюль (гостиная); полиэстер 100 %; цвет Tikkurila V503; карниз 2250 мм, высота 2610 мм, сборка 2,5			аналог по характеристикам	шт.	1		пом. 6
Т15	Римская штора (кухня); лён 100 %; цвет Tikkurila V484; карниз 1400 мм, высота 1620 мм			аналог по характеристикам	шт.	1		пом. 6
Т16	Ковёр в зоне отдыха; шерсть 100 %; цвет Tikkurila V484; 3000×1150 мм			аналог по характеристикам	шт.	1		пом. 6; с подложкой
Т17	Подушки на диван; букле (шерсть 60 %, полиэстер 40 %); цвет Tikkurila H487			аналог по характеристикам	шт.	3		пом. 6
Т18	Подушки на диван, акцент; хлопковый бархат 100 %; цвет Farrow & Ball No. 30			аналог по характеристикам	шт.	2		пом. 6
Т19	Плед на диван; альпака 50 %, шерсть 50 %; цвет Tikkurila V484			аналог по характеристикам	шт.	1		пом. 6
	Декор							
ДК1	Картина над кроватью: абстракция, холст, тонкая рама из дуба; 1200×700 мм; низ на 1300 мм от пола			аналог по характеристикам	шт.	1	4	пом. 1; крепление к стене
ДК2	Зеркало над умывальником, влагостойкое; 600×750 мм; низ на 1100 мм от пола			аналог по характеристикам	шт.	1	4	пом. 2; крепление к стене
ДК3	Картина над кроватью: графика в паспарту, рама — дуб; 1000×700 мм; низ на 1300 мм от пола			аналог по характеристикам	шт.	1	4	пом. 4; крепление к стене
ДК4	Зеркало в рост в тонкой чёрной раме; рама — чёрный матовый; 600×1600 мм; низ на 300 мм от пола			аналог по характеристикам	шт.	1	12	пом. 4; крепление: анкер для пустотелых оснований, 4 шт.
ДК5	Зеркало; рама — чёрный матовый; 800×1800 мм; низ на 550 мм от пола			аналог по характеристикам	шт.	1	18	пом. 5; крепление: анкер, 4 шт.
ДК6	Картина: крупная абстракция в тёплой гамме, холст на подрамнике; 1200×900 мм; центр на 1550 мм от пола			аналог по характеристикам	шт.	1	6	пом. 6; крепление: анкер, 2 шт.
ДК7	Растение в кашпо; 450×450 мм			аналог по характеристикам	шт.	1		пом. 6
ДК8	Ваза керамическая с ветками на обеденном столе; 200×350 мм; на M_18			аналог по характеристикам	шт.	1		пом. 6
ДК9	Зеркало над умывальником, влагостойкое; 500×700 мм; низ на 1100 мм от пола			аналог по характеристикам	шт.	1	4	пом. 7; крепление к стене

						Проект: Трёхкомнатная квартира		
	Лист	№ док.	Подпись	Дата	Спецификация мебели и оборудования (продолжение)	Стадия	Лист	Листов
Дизайнер	Кырпан А.С.			05.10.26		П	12	88

выпуск 05.10.2026 № 204f23b33a · стр. 12 из 88

Ведомость изделий

Марка	Наименование	Пом.	Ш×Г×В, мм	Корпус	Фасад	Кромка, мм скр./вид.	Кол.
М_05	Шкаф распашной	1	1900×600×2400	ЛДСП 16	МДФ 18, эмаль матовая	0,4 / 2	1
М_07	Система хранения	3	1700×600×2400	ЛДСП 16	без фасадов; ящики — МДФ 18, эмаль матовая	0,4 / 2	1
М_13	Шкаф-купе	5	1800×600×2600	ЛДСП 16	рифлёные панели МДФ в алюминиевом профиле	0,4 / 2	1
М_22	Модуль нижний: карго, духовой шкаф, ящики, варочная	6	1800×600×900	ЛДСП 16	МДФ 18, эмаль матовая	0,4 / 2	1
М_24	Модуль навесной: полки	6	600×400×600	ЛДСП 16	МДФ 18, эмаль матовая	0,4 / 2	1
М_23	Модуль навесной: полки, сушка	6	2200×350×720	ЛДСП 16	МДФ 18, эмаль матовая	0,4 / 2	1
М_21	Модуль нижний: ПММ	6	600×600×900	ЛДСП 16	МДФ 18, эмаль матовая	0,4 / 2	1
М_20	Модуль нижний: мойка	6	800×600×900	ЛДСП 16	МДФ 18, эмаль матовая	0,4 / 2	1
М_19	Пенал: холодильник встр.	6	600×650×2100	ЛДСП 16	МДФ 18, эмаль матовая	0,4 / 2	1

Ведомость встраиваемой техники

Поз.	Прибор	Ниша, вырез, мм	Вентиляция	Питание	Схема
М_22.2	Духовой шкаф встраиваемый, 60 см	ниша 560 × 595, глубина ≥ 550	зазор за шкафом, вырез в задней стенке	вывод кабеля под шкафом	по модели
М_22.2	Варочная панель индукционная, 60 см	вырез в столешнице 560 × 490		вывод кабеля под модулем	по модели
М_21	Посудомоечная машина встраиваемая, 60 см	ниша 600 × 862 (от пола до низа столешницы)	зазор в цоколе, по схеме	розетка в соседнем модуле	по модели
М_20	Мойка врезная / подстольная с сифоном	вырез по шаблону, ориентир 700 × 480		смеситель — выводы ВК	по модели
М_19	Холодильник встраиваемый, ниша 1780	ниша 1780 × 560 × 550	решётка в цоколе, канал за корпусом, выход сверху	розетка над нишей или в соседнем модуле	по модели
М_22.2	Вытяжка настенная, 60 см	низ ≥ 650 над панелью	воздуховод к вентканалу, короб до потолка	вывод кабеля в коробе	по модели

Ведомость фурнитуры

№	Фурнитура	Тип, размер	Изделия	Кол.
1	Петля накладная 110° с доводчиком	чашка 35 мм	М_05, М_24, М_23, М_20, М_19	51
2	Полкодержатель с фиксацией	ø5 мм	М_05, М_07, М_13, М_24, М_23, М_19	96
3	Штанга овальная 30×15, L = 926	+ 2 держателя	М_05	1
4	Опора регулируемая с цоколем на клипсах	ход 20 мм	М_05, М_07, М_13	24
5	Анкер по основанию стены	по таблице крепежа	М_05, М_07, М_13, М_24, М_23	28
6	Уголок крепления к стене от опрокидывания	стальной	М_05, М_07, М_13, М_19	8
7	Штанга овальная 30×15, L = 545	+ 2 держателя	М_07	3
8	Система дверей купе: профиль, направляющие, ролики	на 2 двери	М_13	1
9	Ручка-профиль вертикальная	в цвет профиля	М_13	2
10	Штанга овальная 30×15, L = 876	+ 2 держателя	М_13	1
11	Полка для обуви выдвижная наклонная	ширина 876	М_13	3
12	Карго выдвижное 3-уровневое	ширина 350	М_22	1
13	Направляющие полного выдвижения с доводчиком NL 500	пара	М_22	4
14	Ручка-профиль	латунь матовая	М_22, М_24, М_23, М_21, М_20, М_19	19
15	Опора кухонная регулируемая 100–120 мм	+ клипса цоколя	М_22, М_21, М_20, М_19	20
16	Навес регулируемый для навесного шкафа	пара на секцию	М_24, М_23	4
17	Шина монтажная	L = 540	М_24	1
18	Сушка для посуды в шкаф	ширина 800	М_23	1
19	Шина монтажная	L = 2140	М_23	1
20	Комплект навески фасада ПММ	из поставки машины	М_21	1


Примечания

1. Модели техники выбирает заказчик до изготовления мебели; ниши, вырезы и вентиляция — по монтажной схеме выбранной модели (условие гарантии), её номер вносится в ведомость.
2. Количество фурнитуры — по чертежам изделий; запас крепежа 5 %. Аналоги — по характеристикам (доводчик, нагрузка, ход).
3. Цвет корпусов, фасадов и профилей — по колерной карте проекта.


					Проект: Трёхкомнатная квартира			
	Лист	№ док.	Подпись	Дата	Ведомости изделий, техники и фурнитуры	Стадия	Лист	Листов
Дизайнер	Кырпан А.С.			05.10.26		П	13	88

выпуск 05.10.2026 № 204f23b33a · стр. 13 из 88


Фрагмент 1. Ванная (пом. 2)

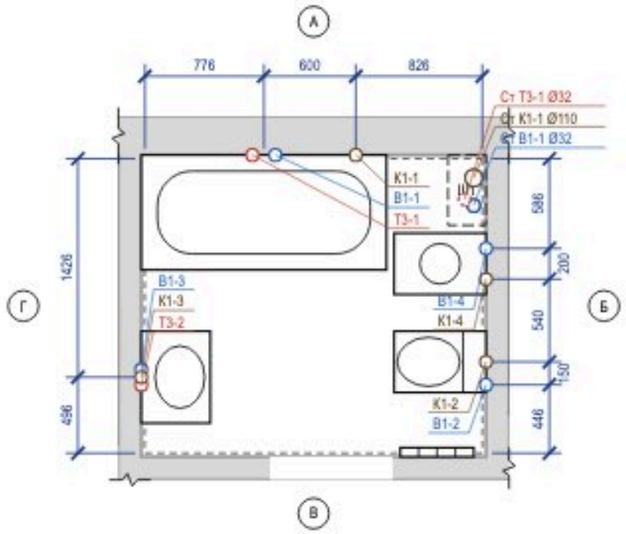

Фрагмент 2. Кухня-гостиная (пом. 6)

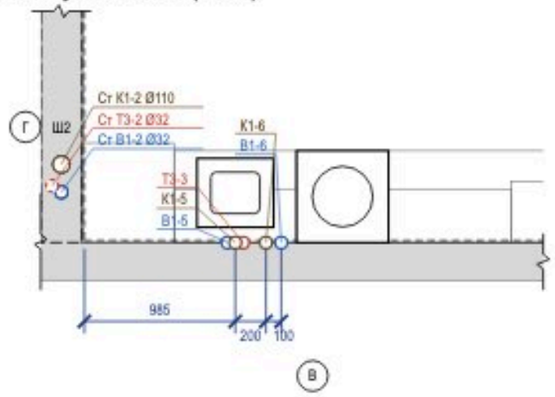

Фрагмент 3. Санузел 2 (пом. 7)

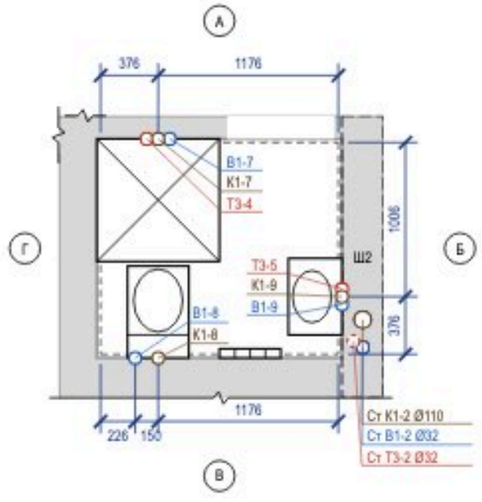

Ведомость привязок выводов

Код	Прибор	Ø	H, мм	Привязка от чист. стен, мм	Прим.
В1-1	С_01 ванна	½"	800	ст. А: 851 от Г	межос. 150
Т3-1	С_01 ванна	½"	800	ст. А: 701 от Г	межос. 150
К1-1	С_01 ванна	Ø50	50	ст. А: 826 от Б	
В1-2	С_02 унитаз подвесной	½"	250	ст. Б: 446 от В	в раме инсталляции
К1-2	С_02 унитаз подвесной	Ø110	220	ст. Б: 596 от В	
В1-3	С_03 умывальник	½"	600	ст. Г: 546 от В	межос. 100
Т3-2	С_03 умывальник	½"	600	ст. Г: 446 от В	межос. 100
К1-3	С_03 умывальник	Ø50	500	ст. Г: 496 от В	
В1-4	ОБ_01 стиральная машина	½"	600	ст. Б: 586 от А	кран машины
К1-4	ОБ_01 стиральная машина	Ø50	600	ст. Б: 786 от А	
В1-5	С_05 мойка кухонная	½"	600	ст. В: 935 от Г	межос. 100
Т3-3	С_05 мойка кухонная	½"	600	ст. В: 1035 от Г	межос. 100
К1-5	С_05 мойка кухонная	Ø50	400	ст. В: 985 от Г	
В1-6	ОБ_03 посудомоечная машина	½"	550	ст. В: 1285 от Г	кран ПММ в шкафу мойки
К1-6	ОБ_03 посудомоечная машина	Ø40	550	ст. В: 1185 от Г	слив ПММ в шкафу мойки
В1-7	С_06 душ	½"	1200	ст. А: 451 от Г	межос. 150
Т3-4	С_06 душ	½"	1200	ст. А: 301 от Г	межос. 150
К1-7	С_06 душ	Ø50	70	ст. А: 376 от Г	сифон поддона
В1-8	С_07 унитаз подвесной	½"	250	ст. В: 226 от Г	в раме инсталляции
К1-8	С_07 унитаз подвесной	Ø110	220	ст. В: 376 от Г	
В1-9	С_08 умывальник	½"	600	ст. Б: 326 от В	межос. 100
Т3-5	С_08 умывальник	½"	600	ст. Б: 426 от В	межос. 100
К1-9	С_08 умывальник	Ø50	500	ст. Б: 376 от В	

Условные обозначения

- вывод В1 (код — в ведомости привязок)
- вывод Т3 (код — в ведомости привязок)
- вывод К1 (код — в ведомости привязок)
- сантехприбор по расстановке (габарит модели)
- чистовая поверхность стены (от неё привязки)
- стояк «Ст К1-N / Ст В1-N» (ГОСТ 21.601), Ø мм
- стояк Т3 не на обмере — принят в шахте рядом со Ст В1, сверить
- шахта / короб стояков, люк 300×400
- линия обрыва (граница фрагмента)
- А — обозначение стены А–Г (как на развёртках)

Примечания

1. Привязки выводов даны от чистовых поверхностей стен (облицовка на сторону: ванная — 24 мм (штукатурка 10 + клей 5 + плитка 9); кухня-гостиная — 24 мм (фартук: штукатурка 10 + клей 5 + плитка 9); санузел 2 — 24 мм (штукатурка 10 + клей 5 + плитка 9)); эти же грани — на развёртках и в раскладке плитки. Высоты — от чистого пола помещения.
2. До черновой разводки сверить по паспорту выбранного прибора (смеситель, инсталляция, сифон).
3. Горячая вода (Т3) — слева от холодной (В1), если смотреть на прибор. Допуск установки выводов: ±5 мм в группе, ±20 мм у отдельно стоящих.
4. Расчёт систем водоснабжения и канализации и подбор оборудования выполняет проектная организация; лист задаёт места и высоты выводов.
5. Посудомоечная машина ОБ_03: кран и слив — отдельными выводами в шкафу мойки (не за машиной), до машины ≤ 1500 мм.
6. Ст Т3-1, Ст Т3-2 на обмере не показаны: приняты рядом с Ст В1-1, Ст В1-2 (в МКД стоят группой); положение сверить на объекте до разметки.
7. Стояки в коробах/шахтах Ш1, Ш2 не замоноличивать; стояк К1 в коробе — звукоизоляция стояка в коробе без жёсткого контакта с трубой; к арматуре и ревизиям — люк не меньше 300×400.

					Проект: Трёхкомнатная квартира
	Лист	№ док.	Подпись	Дата	План выводов сантехники
Дизайнер	Кырпан А.С.			05.10.26	


Стадия	Лист	Листов
П	14	88

выпуск 05.10.2026 № 204f23b33a · стр. 14 из 88


План квартиры (М 1:200)




Фр. 2. Кухня-гостиная (М 1:25)

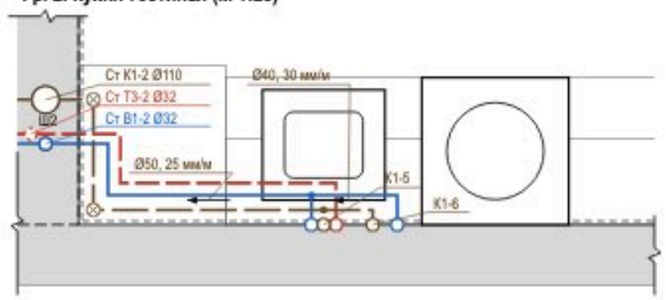

Фр. 1. Ванная (М 1:25)

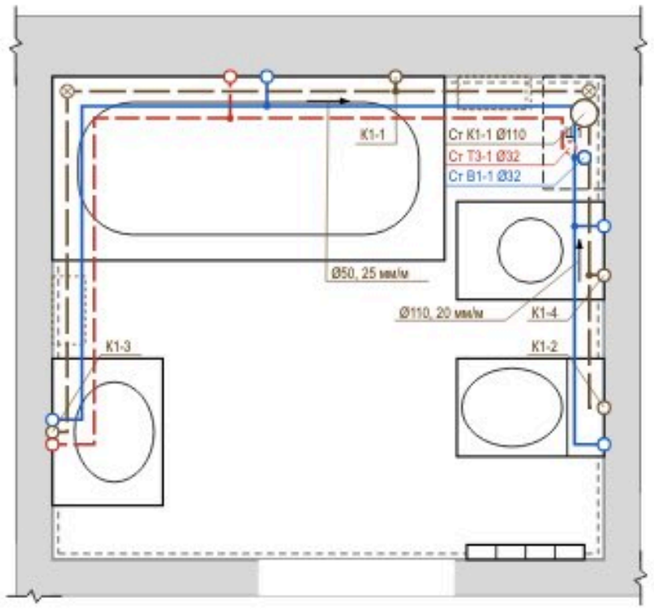

Фр. 3. Санузел 2 (М 1:25)

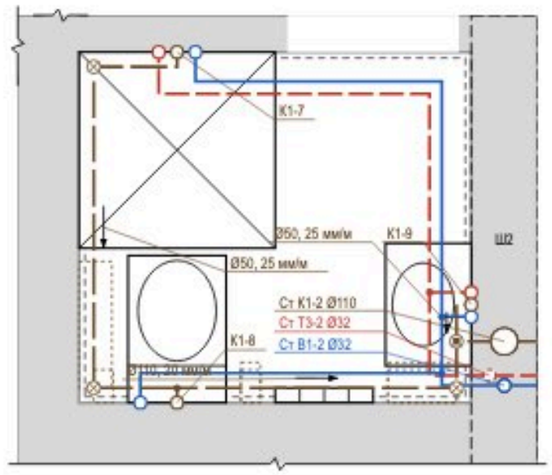

Условные обозначения


- В1 — водопровод хозяйственно-питьевой (ХВС), PP-R Ø20
- Т3 — горячее водоснабжение, подача (ГВС), PP-R Ø20
- К1 — канализация бытовая
- направление уклона К1 / пола: Ø, мм на 1 м
- ⊗ ревизия (прочистка) К1 — доступ сохранить
- • тройник (ответвление к прибору)
- короб К1 над чистым полом (ГКЛВ под плитку)
- ○ вывод В1 (код — в ведомости привязок)
- ○ вывод Т3 (код — в ведомости привязок)
- ○ вывод К1 (код — в ведомости привязок)
- сантехприбор по расстановке (габарит модели)
- ○ стояк «Ст К1-N / Ст В1-N» (ГОСТ 21.601), Ø мм
- ○ стояк Т3 не на обмере — принят в шахте рядом со Ст В1, сверить
- шахта / короб стояков, люк 300×400
- линия обрыва (граница фрагмента)
- граница фрагмента на плане (Фр. N)

Профиль выпусков К1 (до врезки в стояк)

Выпуск	Прибор	Ø	L, м	i, мм/м	Δh, мм	Прокладка, мм
К1-8	С_07 унитаз подвесной	Ø110	1,58	20	32	короб 180×140
К1-2	С_02 унитаз подвесной	Ø110	1,28	20	26	над полом за приборами
К1-3	С_03 умывальник	Ø50	3,69	25	92	короб 180×110
К1-7	С_06 душ	Ø50	3,58	25	89	короб 170×110
К1-5	С_05 мойка кухонная	Ø50	1,65	25	41	над полом за приборами
К1-1	С_01 ванна	Ø50	0,96	25	24	короб 110×110
К1-4	ОБ_01 стиральная машина	Ø50	0,74	25	19	над полом за приборами
К1-9	С_08 умывальник	Ø50	0,41	25	10	над полом за приборами
К1-6	ОБ_03 посудомоечная машина	Ø40	1,84	30	55	над полом за приборами

Короб h×b: h — от чистого пола, b — от чистовой стены. Стяжка 35 мм — лист полов.

Узел ввода В1, Т3 (схема, без масштаба)

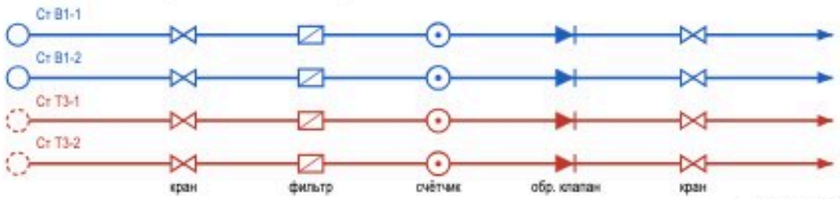

⊗ Ст К1-1, Ст К1-2: ревизия на стояке — люк в коробе

Примечания

1. Трассы принципиальные, построены от стояков вдоль стен помещений; фактическое положение фиксируется исполнительной схемой с привязками (фото с рулеткой) до закрытия.
2. Уклон К1 не менее 1/d и не более 150 мм/м (СП 30.13330.2020, п. 19.1), приняты практические уклоны; поворот — двумя отводами 45°, ревизия после поворота, доступ сохранить. Стояк К1 в коробе — звукоизоляция стояка в коробе, без жёсткого контакта короба с трубой.
3. Решение по К1: стяжка 35 мм не укрывает трубы (нужно Ø + Δh + 45 мм) — выпуски идут над чистым полом вдоль стен: К1-2, К1-5, К1-4, К1-9, К1-6 — за приборами и в раме инсталляции; К1-8, К1-3, К1-7, К1-1 — в коробе ГКЛВ под плитку (размеры в профиле). Короба — на развёртках; отметку низа врезки в стояк замерить до черновых работ.
4. На каждом вводе В1 и Т3 — кран шаровой, фильтр, счётчик, обратный клапан; доступ через люк не меньше 300×400. Водопровод — в штробе стен или в коробах; трубы испытать давлением до закрытия (акт скрытых работ).
5. Расчёт систем, диаметры магистралей и подбор оборудования выполняет проектная организация; врезка и перенос стояков — по согласованию с управляющей организацией. Арматуру и привязки сверить по паспортам приборов.
6. Ст Т3-1, Ст Т3-2 на обмере не показаны: приняты рядом с Ст В1-1, Ст В1-2; положение сверить на объекте до разводки.

					Проект: Трёхкомнатная квартира
	Лист	№ док.	Подпись	Дата	Схема разводки водопровода и канализации
Дизайнер	Кырпан А.С.			05.10.26	

Стадия	Лист	Листов
П	15	88

выпуск 05.10.2026 · № 204f23b33a · стр. 15 из 88


Поз.	Наименование и техническая характеристика	Тип, марка, обозначение документа	Код продукции	Поставщик	Ед. изм.	Кол.	Масса 1 ед., кг	Примечание
	Санитарные приборы							
1	Ванна акриловая 1600×750 мм, с каркасом, экраном и отверстием слив-перелив	аналог		выбор заказчика	шт	1		С_01
2	Унитаз подвесной безободковый, с сиденьем микролифт, крепёж и звукоизолирующая прокладка	аналог		выбор заказчика	шт	2		С_02, С_07
3	Инсталляция для подвесного унитаза: рама высотой 1120 мм, бачок, клавиша смыва (ось клавиши 1050 мм от чистого пола)	аналог		выбор заказчика	шт	2		С_02, С_07; короб ГКЛВ
4	Умывальник подвесной 450×600 мм, с отверстием под смеситель и переливом	аналог		выбор заказчика	шт	1		С_03
5	Умывальник подвесной 350×500 мм, с отверстием под смеситель и переливом	аналог		выбор заказчика	шт	1		С_08
6	Поддон душевой низкий 800×800 мм, с сифоном и выпуском Ø50, на ножках/подиуме	аналог		выбор заказчика	шт	1		С_06
7	Мойка кухонная врезная 500×450 мм, с переливом	аналог		с кухонной мебелью	шт	1		С_05
8	Полотенцесушитель электрический, IP44, с терморегулятором	аналог		выбор заказчика	шт	2		С_04, С_09
	Смесители, сифоны и арматура приборов							
9	Смеситель для ванны настенный однорычажный, межосевое 150 мм, с душевым набором (лейка, шланг, держатель)	аналог		выбор заказчика	шт	1		С_01
10	Смеситель для умывальника однорычажный, с донным клапаном	аналог		выбор заказчика	шт	2		С_03, С_08
11	Душевая система скрытого монтажа с термостатом: встраиваемая часть, верхний душ, ручная лейка	аналог		выбор заказчика	шт	1		С_06; встраиваемая часть — до плитки
12	Смеситель кухонный однорычажный, высокий излив	аналог		выбор заказчика	шт	1		С_05
13	Обвязка ванны слив-перелив Ø40/50 с сифоном	аналог		выбор заказчика	шт	1		С_01
14	Сифон для умывальника бутылочный Ø32/40–50, с гофрой к выпуску	аналог		выбор заказчика	шт	2		С_03, С_08
15	Сифон для мойки с отводом для ПММ Ø40/50	аналог		выбор заказчика	шт	1		С_05
16	Сифон для стиральной машины встраиваемый в стену Ø50, с обратным клапаном	аналог		выбор заказчика	шт	1		СБ_01
17	Кран угловой ½"×½" с гибкой подводкой 40 см (умывальники, мойка)	аналог		выбор заказчика	шт	6		по 2 на прибор
18	Кран шаровой угловой ½"×¾" для подключения стиральной и посудомоечной машины	аналог		выбор заказчика	шт	2		СБ_01, СБ_03
	Трубопроводы							
19	Труба полипропиленовая PP-R PN20 Ø20×3,4 (В1)	ГОСТ 32415-2013		выбор заказчика	м	18,5	0,17	11,2 + 5,5 + 10 %
20	Труба PP-R, армированная стекловолокном, PN20 Ø20×2,8 (Т3)	ГОСТ 32415-2013		выбор заказчика	м	13,5	0,15	8,2 + 3,8 + 10 %
21	Труба канализационная ПП Ø40 (К1)	ГОСТ 32414-2013		выбор заказчика	м	1		0,3 + 0,6 + 10 %
22	Труба канализационная ПП Ø50 (К1)	ГОСТ 32414-2013		выбор заказчика	м	11		7,7 + 2,1 + 10 %
23	Труба канализационная ПП Ø110 (К1)	ГОСТ 32414-2013		выбор заказчика	м	4		2,9 + 0,4 + 10 %
	Фасонные части и выводы							
24	Отвод канализационный ПП 45° Ø40	ГОСТ 32414-2013		выбор заказчика	шт	2		2 шт. на поворот
25	Отвод канализационный ПП 45° Ø50	ГОСТ 32414-2013		выбор заказчика	шт	20		2 шт. на поворот
26	Отвод канализационный ПП 45° Ø110	ГОСТ 32414-2013		выбор заказчика	шт	10		2 шт. на поворот
27	Тройник канализационный ПП 45° (врезки ветвей)	ГОСТ 32414-2013		выбор заказчика	шт	8		
28	Ревизия канализационная ПП (после поворота трассы)	ГОСТ 32414-2013		выбор заказчика	шт	9		доступ сохранить
29	Фитинги PP-R Ø20: тройники, угольники 90° (ветви и повороты В1, Т3)	ГОСТ 32415-2013		выбор заказчика	шт	34		
30	Водорозетка PP-R Ø20×½" настенная, с креплением	ГОСТ 32415-2013		выбор заказчика	шт	14		коды — лист выводов
	Узлы ввода, люки, короба							
31	Кран шаровой латунный Ду15 PN16 (отключение ввода)	аналог		выбор заказчика	шт	4		Ст В1-1, Ст В1-2, Ст Т3-1, Ст Т3-2
32	Фильтр сетчатый косой Ду15	аналог		выбор заказчика	шт	4		
33	Счётчик воды крыльчатый Ду15 (ХВ, ГВ), с поверкой	аналог		выбор заказчика	шт	4		пломба УК
34	Клапан обратный Ду15	аналог		выбор заказчика	шт	4		
35	Люк ревизионный накимной под плитку 300×400 мм	аналог		выбор заказчика	шт	2		к стоякам и арматуре
36	Звукоизоляция стояка К1 в коробе: рулонный звукоизоляционный материал ≥ 10 мм, обмотка стояка на высоту этажа	аналог		выбор заказчика	м	5,4		Ст К1-1, Ст К1-2
37	Короб К1 над полом: профиль ПНПС, ГКЛВ 12,5 мм под плитку	аналог		выбор заказчика	м	2,4		сечение — лист разводки

Примечания

1. Форма 1 ГОСТ 21.110-2013, ширины граф изменены по п. 4.1. «Аналог» — аналог по характеристикам: модели внести до черновых работ, привязки выводов сверить по паспортам.
2. Бытовая техника не входит (показана арматура подключения), мойка — в комплекте кухни. Длины труб — трасса листа разводки + подъёмы + 10 %.
3. Стояк К1 в коробе — звукоизоляция стояка в коробе без жёсткого контакта короба с трубой.
4. Расчёт систем водоснабжения и канализации, диаметры магистралей и подбор оборудования выполняет проектная организация.

					Проект: Трёхкомнатная квартира			
	Лист	№ док.	Подпись	Дата	Спецификация сантехнического оборудования	Стадия	Лист	Листов
Дизайнер	Кырпан А.С.			05.10.26		П	16	88

выпуск 05.10.2026 № 204f23b33a · стр. 16 из 88

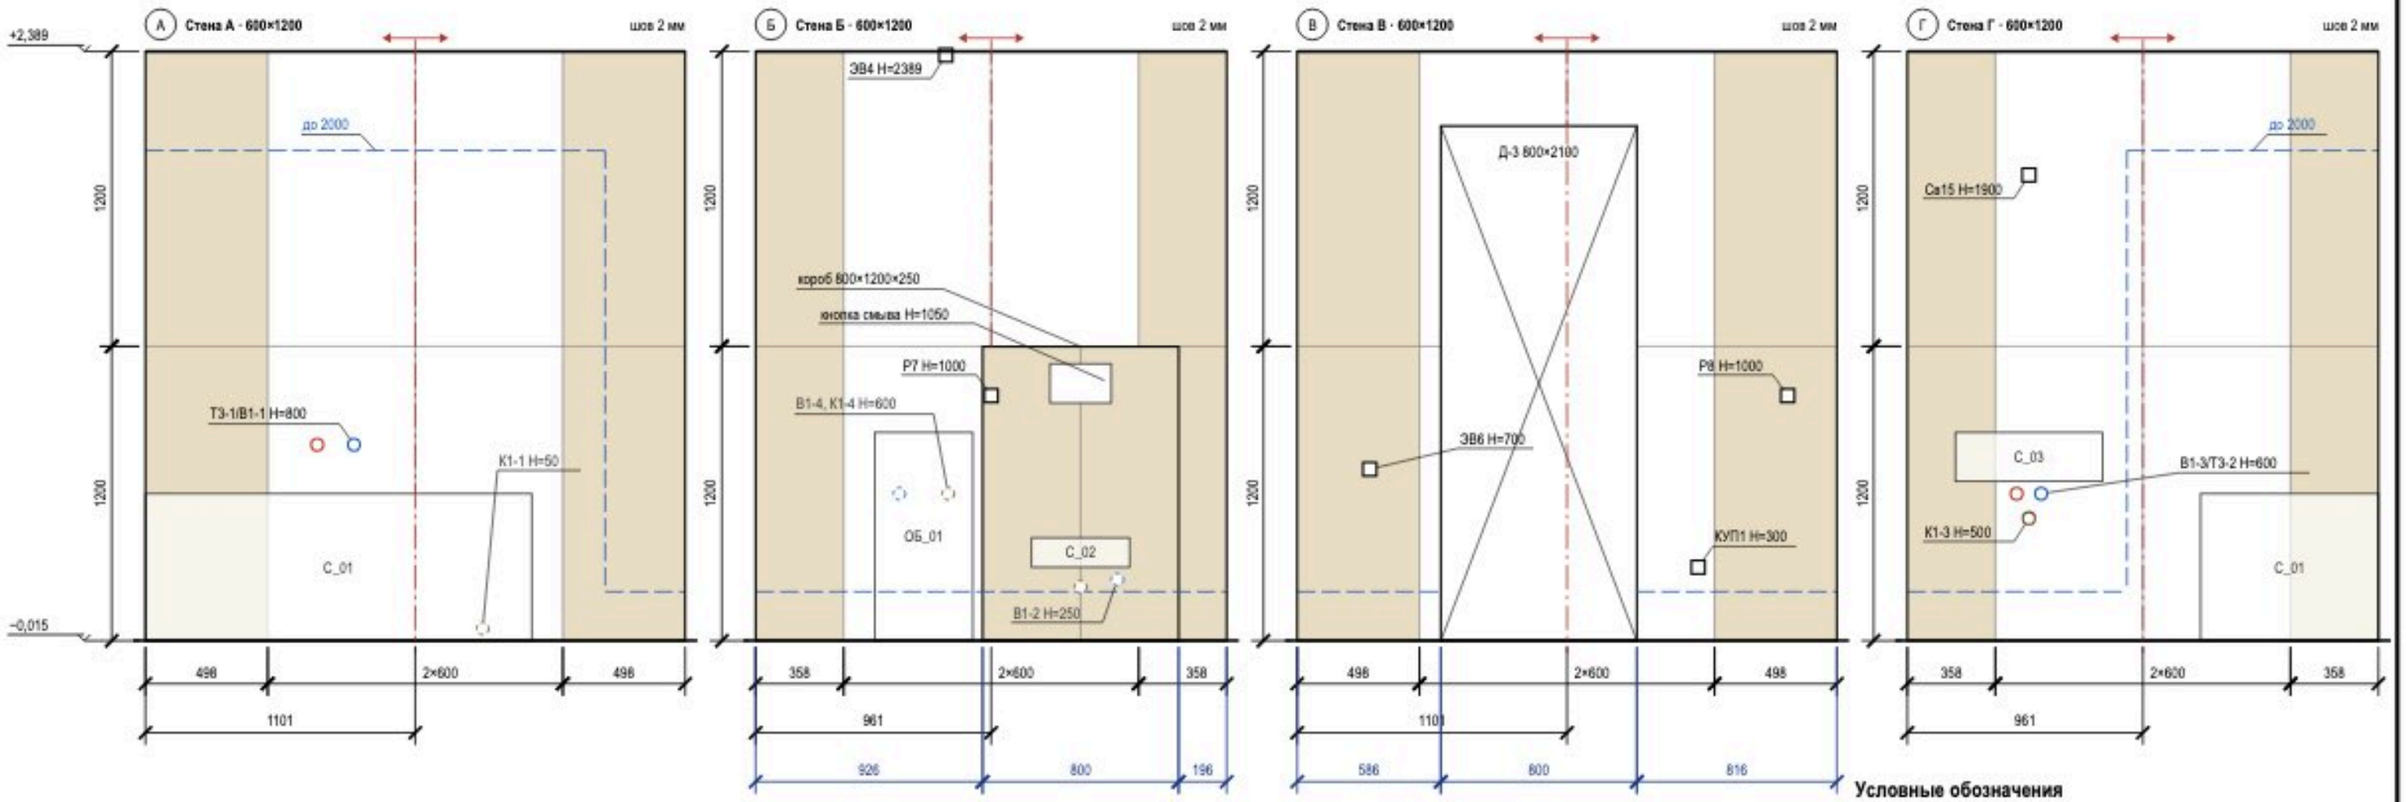

Подсчёт плитки по стенам и коробу

Поверхность	L × H, мм	S, м²	Целых	Подр.	С запасом	Подрезки: край / верх, мм
стена А	2202 × 2404	5,41	4	4	9	498 / 498; целый ряд
стена Б	1922 × 2404	3,78	2	6	8	358 / 358; целый ряд
короб (ст. Б)	800×1200×250	1,76	0	6	7	лицо 399 / 399; бок. 250
стена В	2202 × 2404	3,73	0	8	9	498 / 498; целый ряд
стена Г	1922 × 2404	4,74	4	4	9	358 / 358; целый ряд
Итого		**19,41**	**10**	**27**	**42**	

Сдвиг точек под раскладку

Точка (ВК, ЭОМ)	Стена	Проект: от угла / Н	Под раскладку: от угла / Н	Сдвиг, мм
Т3-1/В1-1	А	776 / 800	800 / 800	+24 в центр плитки
ЭВ4	Б	776 / 2389	660 / 2403	−116 в центр плитки; Н +14
КУП1	В	1636 / 300	1703 / 300	+67 на шов
ЭВ6	В	296 / 700	198 / 700	−98 в центр плитки
В1-3/Т3-2, К1-3, Св15	Г	496 / 600, 500, 1900	359 / 600, 500, 1900	−137 на шов

Примечания

1. Вид изнутри, стены по часовой стрелке А → Г. Высоты — от чистого пола (−0,015), отметки — от ±0,000. Раскладка от чистовых размеров (штукатурка 10 + клей 5 + плитка 9 мм), подрезки чистые; старт — от оси стены, ряды от пола целыми.
2. Облицовка до потолка (+2,389).
3. Точки из таблицы сдвигов переносятся до черновой разводки: смеситель — по оси пары В1 + Т3; вывод на оси прибора — вместе с прибором, иначе старт раскладки — на ось прибора.
4. За приборами и в коробе (К1-1, В1-2, К1-2, В1-4, К1-4) — штрмховым кольцом.
5. Гидроизоляция: 200 мм от ЧП по периметру; над ванной — до 2000 и 300 мм за борт (СП 29.13330.2011, п. 7.2 — на высоту замачивания); углы — лентой; акт скрытых работ, пролив.
6. Короб 800×1200×250: лицо 399 / 399 мм от оси кнопки смыва, боковины, полка; углы — запил 45° или профиль; за коробом плитку не кладут.
7. Между коробом и углом полоса 196 мм — довести короб до угла.


Условные обозначения


- плитка целая; тонкая линия — шов
- плитка с подрезкой (размер — на цепочке)
- ось старта; стрелки — направление укладки
- верх гидроизоляции: 200 от ЧП, в мокрой зоне — «до …»
- проём — не облицовывается
- сантехприбор: габарит, высота по практике
- короб инсталляции, в нём кнопка смыва 250×160
- вывод В1 (код — в ведомости привязок)
- вывод Т3 (код — в ведомости привязок)
- вывод К1 (код — в ведомости привязок)
- вывод за прибором / в коробе (не на сетке)
- электроточка: марка и Н — по листам ЭОМ
- отметка уровня, м: ±0,000 — чистый пол жилых помещений
- низ потолка; серая полоса — стена без плитки
- (А) обозначение стены А–Г (как на развёртках)


					Проект: Трёхкомнатная квартира
	Лист	№ док.	Подпись	Дата	Раскладка плитки. Ванная. Развёртки стен
Дизайнер	Кырпан А.С.			05.10.26	


Стадия	Лист	Листов
П	17	88

выпуск 05.10.2026 № 204f23b33a · стр. 17 из 88

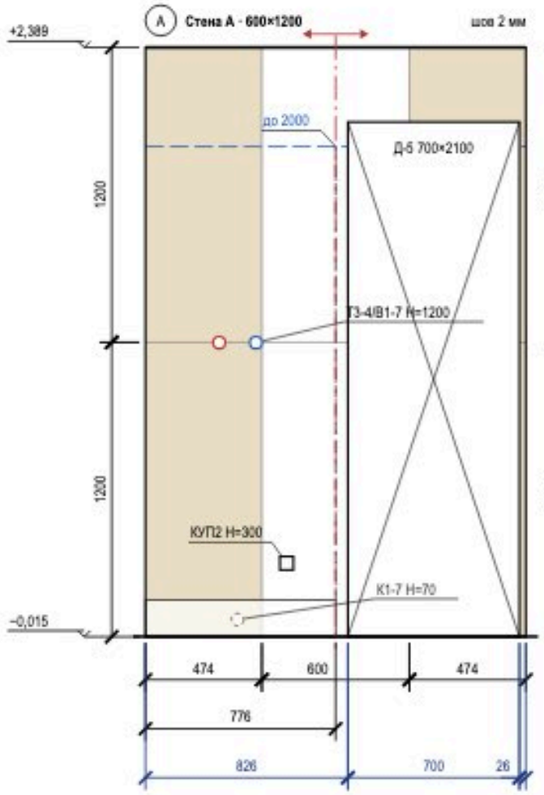

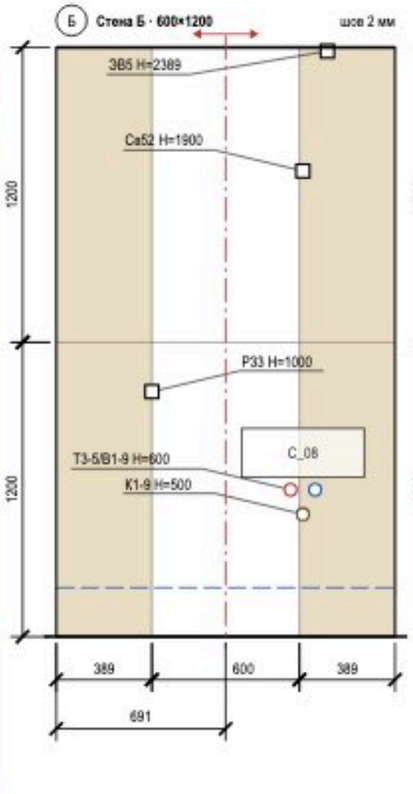

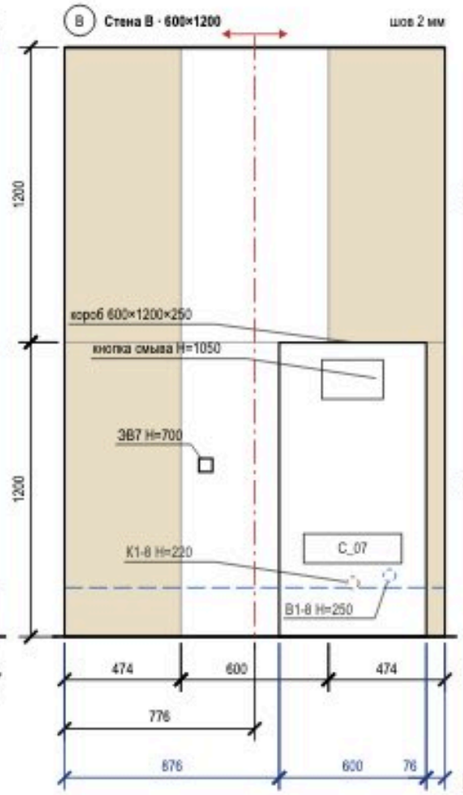

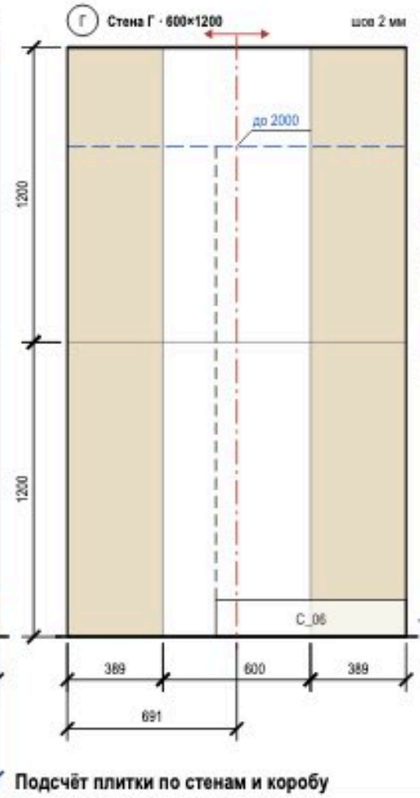

Условные обозначения

- плитка целая; тонкая линия — шов
- плитка с подрезкой (размер — на цепочке)
- ось старта; стрелки — направление укладки
- верх гидроизоляции: 200 от ЧП, в мокрой зоне — «до …»
- проём — не облицовывается
- сантехприбор: габарит, высота по практике
- граница душевой зоны (ограждение)
- короб инсталляции, в нём кнопка смыва 250×160
- вывод В1 (код — в ведомости привязок)
- вывод Т3 (код — в ведомости привязок)
- вывод К1 (код — в ведомости привязок)
- вывод за прибором / в коробе (не на сетке)
- электроточка: марка и Н — по листам ЭОМ
- отметка уровня, м: ±0,000 — чистый пол жилых помещений
- низ потолка; серая полоса — стена без плитки
- (А) обозначение стены А–Г (как на развёртках)

Подсчёт плитки по стенам и коробу

Поверхность	L × H, мм	S, м²	Целых	Подр.	С запасом	Подрезки: край / верх, мм
стена А	1552 × 2404	2,38	0	6	7	474 / 474; цельный ряд
стена Б	1382 × 2404	3,44	2	4	7	389 / 389; цельный ряд
стена В	1552 × 2404	3,13	1	5	7	474 / 474; цельный ряд
короб (ст. В)	600×1200×250	1,47	1	3	5	лицо 600; бок. 250
стена Г	1382 × 2404	3,44	2	4	7	389 / 389; цельный ряд
Итого		**13,85**	**6**	**22**	**33**	

Сдвиг точек под раскладку

Точка (ВК, ЭОМ)	Стена	Проект: от угла / Н	Под раскладку: от угла / Н	Сдвиг, мм
Т3-4/В1-7	А	376 / 1200	475 / 1141	+99 на шов; Н −59
КУП2	А	576 / 300	475 / 300	−101 на шов
Т3-5/В1-9, К1-9, Са52	Б	1006 / 600, 500, 1900	992 / 600, 500, 1900	−14 на шов
ЭВ5	Б	1106 / 2389	992 / 2343	−114 на шов; Н −46
ЭВ7	В	576 / 700	475 / 700	−101 на шов


Примечания

1. Вид изнутри, стены по часовой стрелке А → Г. Высоты — от чистого пола (−0,015), отметки — от ±0,000. Раскладка от чистовых размеров (штукатурка 10 + клей 5 + плитка 9 мм), подрезки чистые; старт — от оси стены, ряды от пола целыми.
2. Облицовка до потолка (+2,389).
3. Точки из таблицы сдвигов переносятся до черновой разводки: смеситель — по оси пары В1 + Т3; вывод на оси прибора — вместе с прибором, иначе старт раскладки — на ось прибора.
4. За приборами и в коробе (К1-7, В1-8, К1-8) — штраховым кольцом.
5. Гидроизоляция: 200 мм от ЧП по периметру; у душа — до 2000 и 500 мм за поддон (СП 29.13330.2011, п. 7.2 — на высоту замачивания); углы — лентой; акт скрытых работ, прогив.
6. Короб 600×1200×250: лицо 600 мм от оси кнопки смыва, боковины, полка; углы — запил 45° или профиль; за коробом плитку не кладут.
7. Между коробом и углом полоса 76 мм — довести короб до угла.

					Проект: Трёхкомнатная квартира
	Лист	№ док.	Подпись	Дата	Раскладка плитки. Санузел 2. Развёртки стен
Дизайнер	Кырпан А.С.			05.10.26	

Стадия	Лист	Листов
П	18	88

выпуск 05.10.2026 № 204f23b33a · стр. 18 из 88

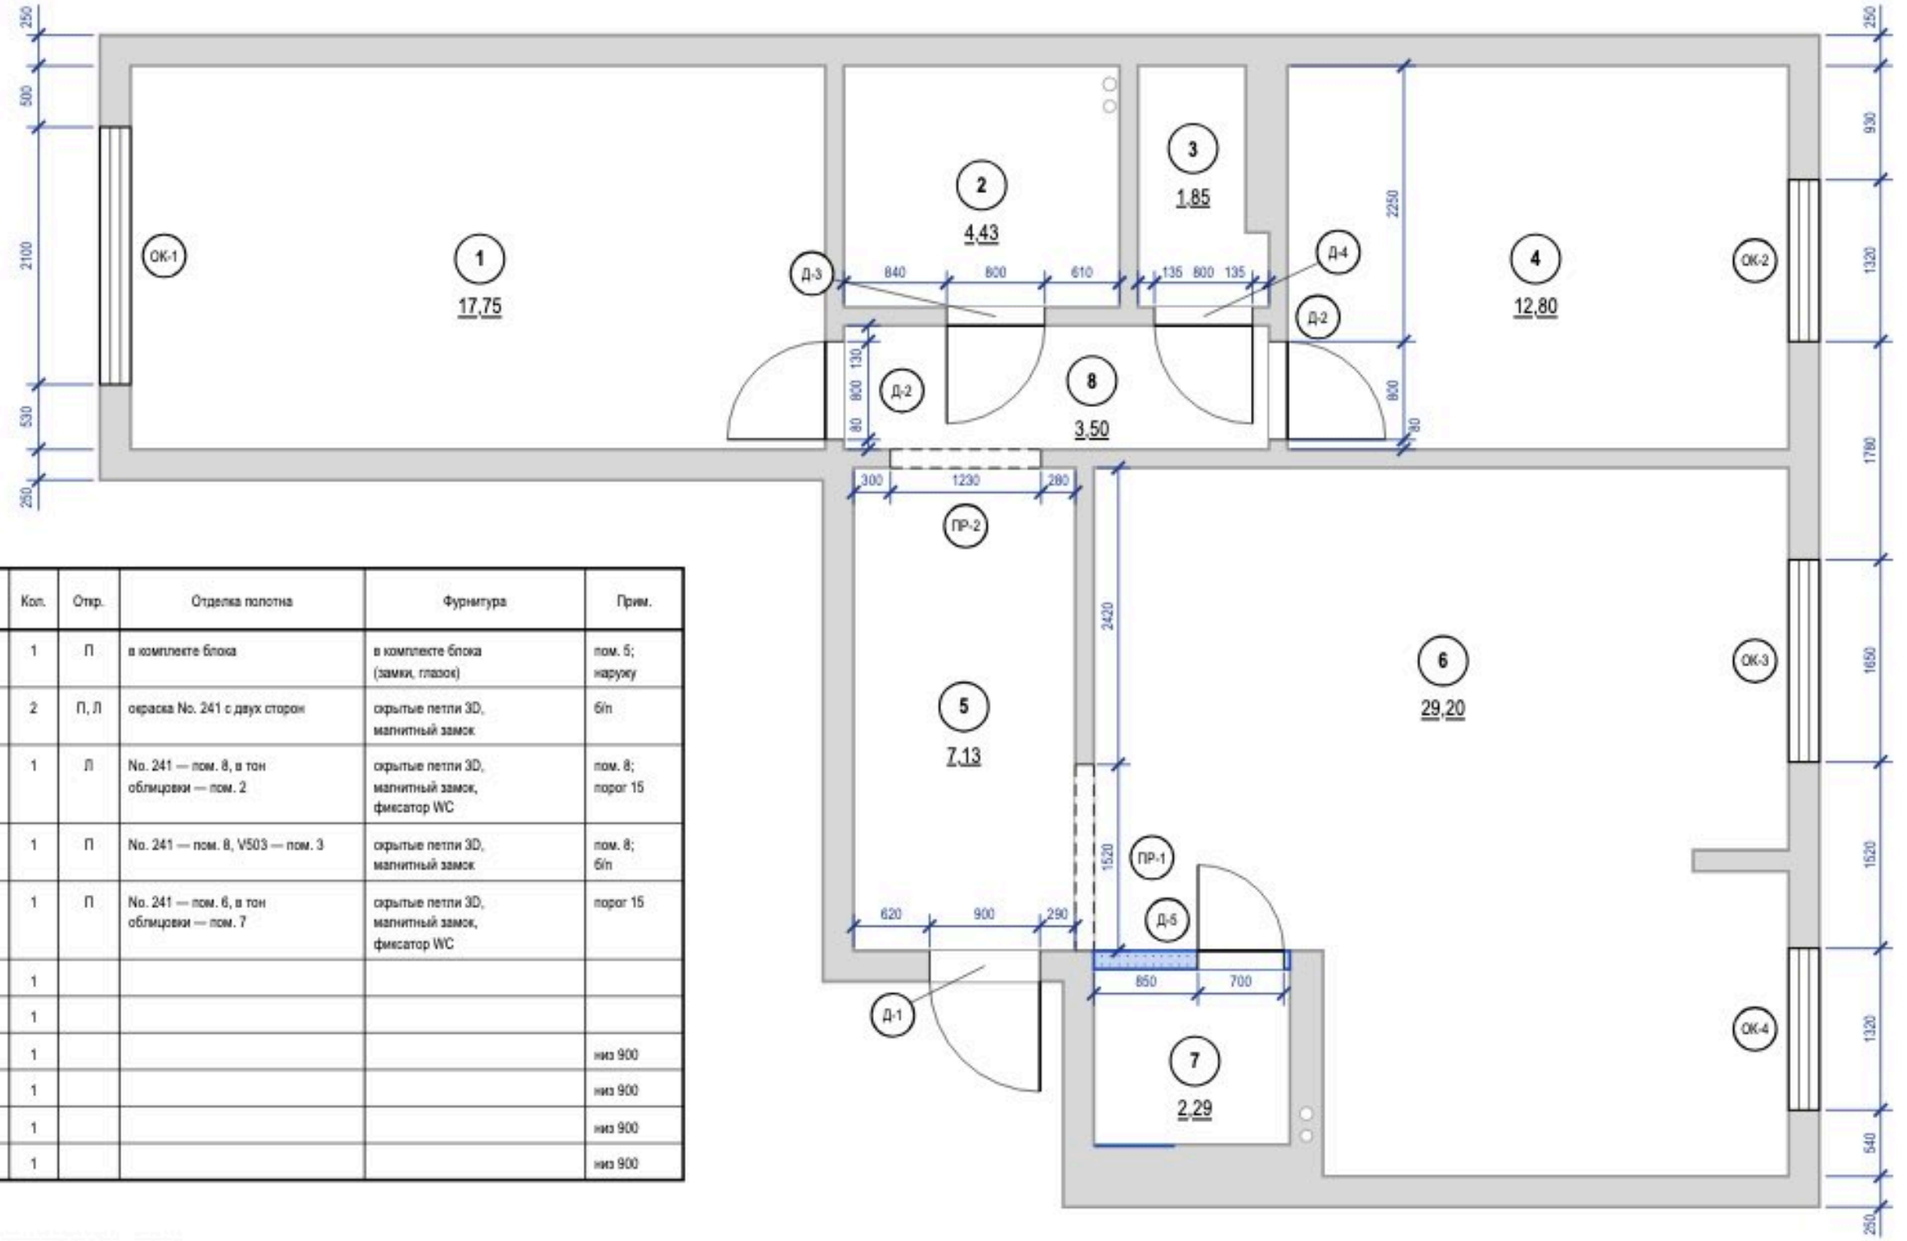

Ведомость заполнения проёмов


Марка	Наименование, обозначение	Проём ш×в, мм	Кол.	Откр.	Отделка полотна	Фурнитура	Прим.
Д-1	Блок дверной входной, ГОСТ 31173-2016	900×2100	1	П	в комплекте блока	в комплекте блока (замки, глазок)	пом. 5; наружу
Д-2	Дверь скрытого монтажа, ТУ изготовителя	800×2100	2	П, Л	окраска No. 241 с двух сторон	скрытые петли 3D, магнитный замок	б/п
Д-3	Дверь скрытого монтажа, ТУ изготовителя	800×2100	1	Л	No. 241 — пом. 8, в тон облицовки — пом. 2	скрытые петли 3D, магнитный замок, фиксатор WC	пом. 8; порог 15
Д-4	Дверь скрытого монтажа, ТУ изготовителя	800×2100	1	П	No. 241 — пом. 8, V503 — пом. 3	скрытые петли 3D, магнитный замок	пом. 8; б/п
Д-5	Дверь скрытого монтажа, ТУ изготовителя	700×2100	1	П	No. 241 — пом. 6, в тон облицовки — пом. 7	скрытые петли 3D, магнитный замок, фиксатор WC	порог 15
ПР-1	Портал без заполнения	1520×2500	1				
ПР-2	Портал без заполнения	1230×2100	1				
ОК-1	Блок оконный существующий	2100×1500	1				низ 900
ОК-2	Блок оконный существующий	1320×1500	1				низ 900
ОК-3	Блок оконный существующий	1650×1500	1				низ 900
ОК-4	Блок оконный существующий	1320×1400	1				низ 900

Примечания

1. Размеры проёмов и привязки — в миллиметрах от чистых граней стен до отделки; привязка — от угла того помещения, со стороны которого стоит размер. Размер в ведомости — ширина × высота проёма от чистого пола 0,000. Откос от угла помещения до проёма с коробкой — не менее 50 мм.
2. Марки в кружках — типы заполнения проёмов (ГОСТ 21.501-2018, п. 5.3.2); одна марка — один типоразмер; количество сверено с планом.
3. Открывание: Л — петли слева, П — справа, если смотреть со стороны, куда открывается полотно (на себя).
4. Скрытые двери (Д-2…Д-5): проём замерить в чистоте; блок заказать до штукатурки (≈ 30 дн.), короб ставить до штукатурки; полотно навесить после чистовой отделки, красить в цвет стен. Порядок практика монтажа, изготовитель подтверждает.
5. Д-2…Д-4 — существующие проёмы, до техзаключения не расширять. Д-3, Д-4: стена принята 150 мм, по скану 85 мм, не замерено; узел — для 150 мм.
6. Окна ОК-1…ОК-4 существующие, сохраняются; подоконники и откосы не заданы — приняты.
7. Размеры проёмов и привязки сняты со скана плана заказчика и на объекте не замерены (обмерный план — лист 3).
8. Экспликация помещений — лист 3; в марках помещений — номер и площадь, м².
9. Привязка проёма к углу помещения меньше 1 мм на листе, размер на плане не показан: Д-5 — 50 мм.

					Проект: Трёхкомнатная квартира	
	Лист	№ док.	Подпись	Дата		
Дизайнер	Кырпан А.С.			05.10.26	План размещения дверей	Стадия: П; Лист: 19; Листов: 88

выпуск 05.10.2026 № 204f23b33a · стр. 19 из 88

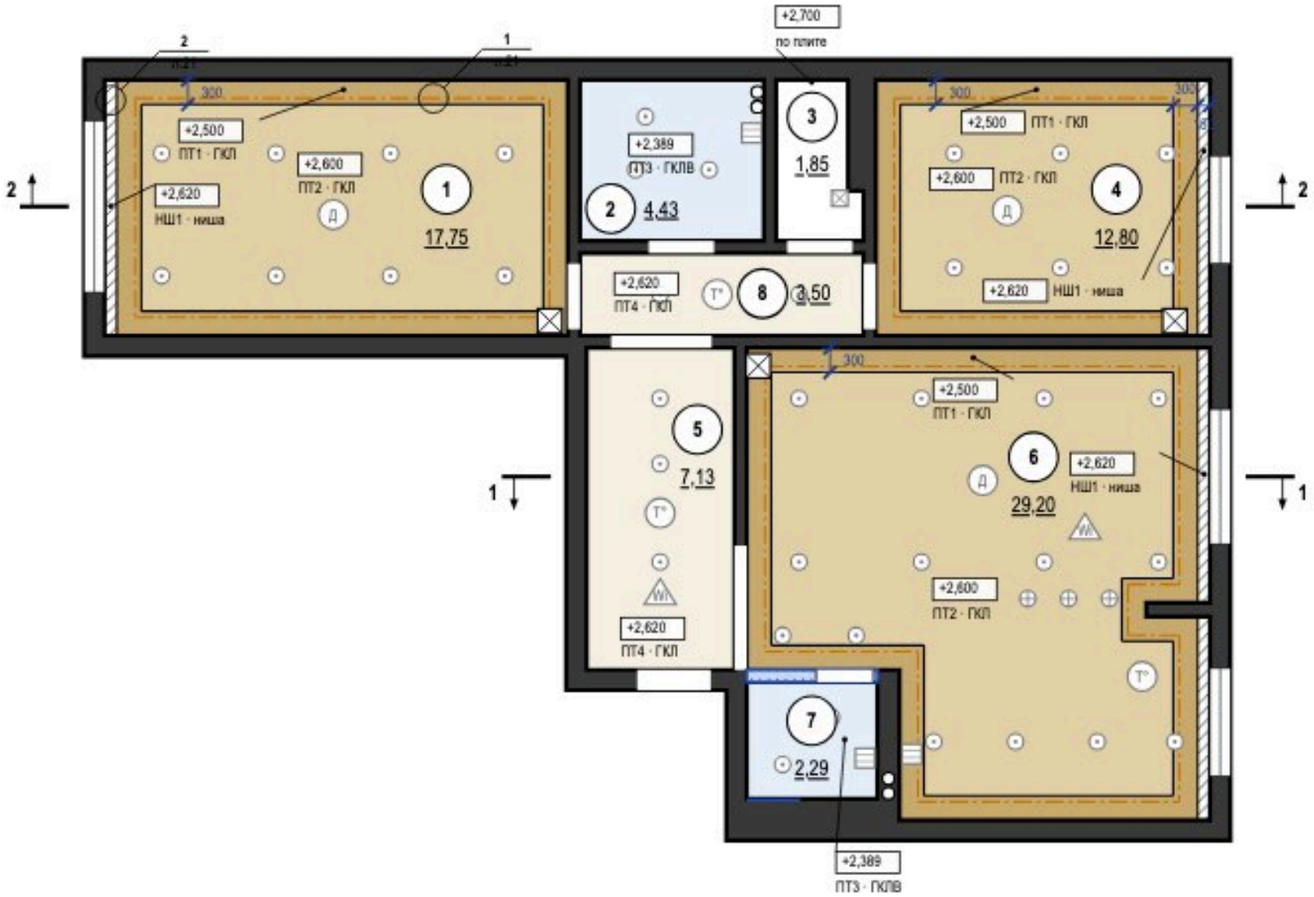

Ведомость потолков

Пом.	Марка	Конструкция	Низ	S, м²	Q
1	ПТ1	ГКЛ П113, короб LED	+2,500	4,83	Q3
1	ПТ2	ГКЛ П113	+2,600	12,45	Q3
1	НШ1	ниша под шторы 150×120	+2,620	0,47	
2	ПТ3	ГКЛВ П113	+2,389	4,43	Q3
3		по плите, окраска	+2,700	1,85	
4	ПТ1	ГКЛ П113, короб LED	+2,500	3,88	Q3
4	ПТ2	ГКЛ П113	+2,600	8,45	Q3
4	НШ1	ниша под шторы 150×120	+2,620	0,47	
5	ПТ4	ГКЛ П113	+2,620	7,13	Q3
6	ПТ1	ГКЛ П113, короб LED	+2,500	6,80	Q3
6	ПТ2	ГКЛ П113	+2,600	21,56	Q3
6	НШ1	ниша под шторы 150×120	+2,620	0,84	
7	ПТ3	ГКЛВ П113	+2,389	2,29	Q3
8	ПТ4	ГКЛ П113	+2,620	3,50	Q3
		Итого		**78,95**	

Ведомость вырезов и закладных в потолке

Марка	Устройство	Кол.	Пом.
	Светильник встраиваемый (марки — план освещения)	39	1, 2, 4, 5, 6, 7, 8
	Светильник накладной (марки — план освещения)	1	3
	Светильник подвесной (марки — план освещения)	3	6
ИП1, ИП2, ИП4	Извещатель дымовой	3	1, 4, 6
ИП3, ИП5, ИП6	Извещатель тепловой	3	5, 6, 8
АР1, АР2	Точка доступа Wi-Fi, PoE	2	5, 6
ВР1…ВР3	Решётка вытяжная (вентилятор)	3	2, 6, 7
	Люк ревизии 300×300	3	1, 4, 6

Примечания

1. За отметку ±0,000 принят уровень чистого пола сухих помещений (готовое покрытие), а не существующего пола; пол пом. 2, 7 — −0,015; верх плиты перекрытия −0,064 — расчётный по пирогу пола, не замерен; существующий пол снимается до плиты, его отметка не замерена. Отметки в прямоугольниках — низ потолка; низ плиты перекрытия +2,700. Марка потолка — одна конструкция и отметка на весь альбом.
2. Потолки ГКЛ — каркасная система П113: подвесы через 1000, несущие профили через 500, основные через 1200 мм; листы — поперёк несущих профилей. В помещениях 2, 7 — ГКЛВ на оцинкованном каркасе.
3. Нижний уровень — пояс-короб по периметру шириной 300 мм (карниз подсветки + 150 мм полки), верхний — поле внутри пояса.
4. LED-лента в алюминиевом профиле посередине карниза короба шириной 300 мм (узел 1, лист 21); длина по плану: пом. 1 — 15,5 м (в плане освещения 15,5); пом. 4 — 12,3 м (в плане освещения 12,3); пом. 6 — 22,1 м (в плане освещения 22,1).
5. Ниши под шторы 150×120 мм — на всю длину стены с окном; карниз — на закладной до обшивки (узел 2, лист 21).
6. Примыкание к стенам: теневой шов 15 мм, техзазор 3 мм — пом. 1, 4, 6, по стенам, выровненным штукатуркой (узел 1); пом. 2, 5, 7, 8 разделительная лента.
7. Светильники и потолочные устройства — подложка с планов освещения, слаботочных систем и вентиляции (положение — по ним); вырезы и закладные — по ведомости на листе, до обшивки; отверстия не совмещать с профилями, глубина корпуса светильника до 70 мм.
8. Разрезы 1–1, 2–2 и узлы — на листе 21; высоты мебели и дверных блоков сверены с низом потолка в разрезах.
9. Шпаклевание ГКЛ и условия приёмки — Q3: рассеянный дневной свет, осмотр с 2 м; боковой свет не оценивается.
10. Люки ревизии 300×300 мм — по центру блоков питания LED (БП1, БП2, БП4; координаты — план освещения).
11. Пом. 3 — потолок по плите без подвесной системы; отделка — по ведомости отделки.


					Проект: Трёхкомнатная квартира
	Лист	№ док.	Подпись	Дата	
Дизайнер	Кырпан А.С.			05.10.26	План потолков

Стадия	Лист	Листов
П	20	88

выпуск 05.10.2026 № 204f23b33a · стр. 20 из 88


Разрез 1–1 (М 1:40)

Пом. 6 Кухня-гостиная; линия разреза — план потолков, лист 20

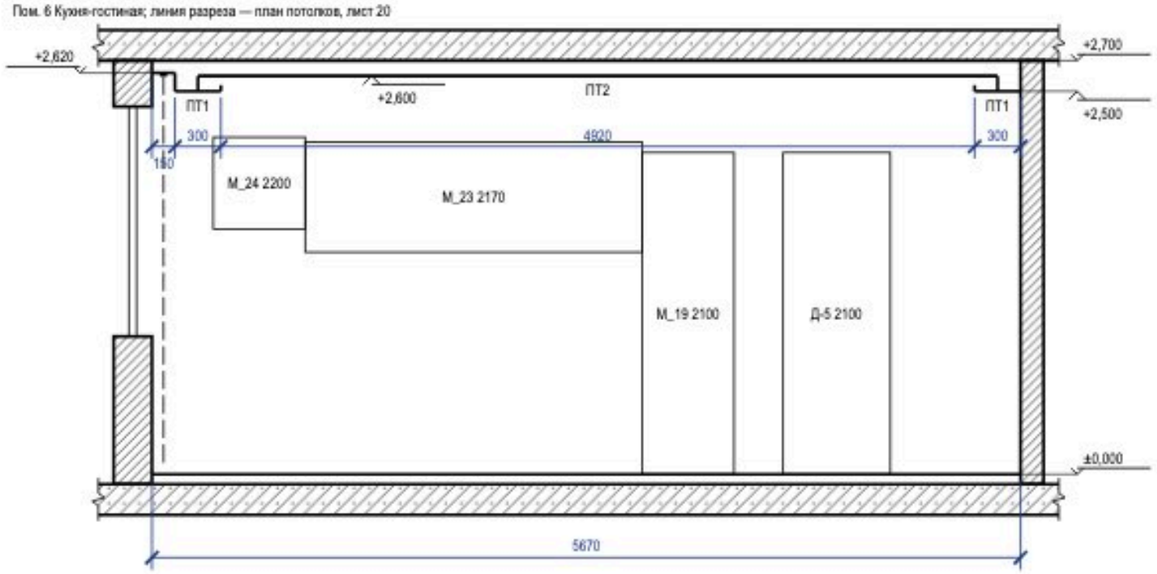


Разрез 2–2 (М 1:40)

Пом. 1 Спальня 1; линия разреза — план потолков, лист 20

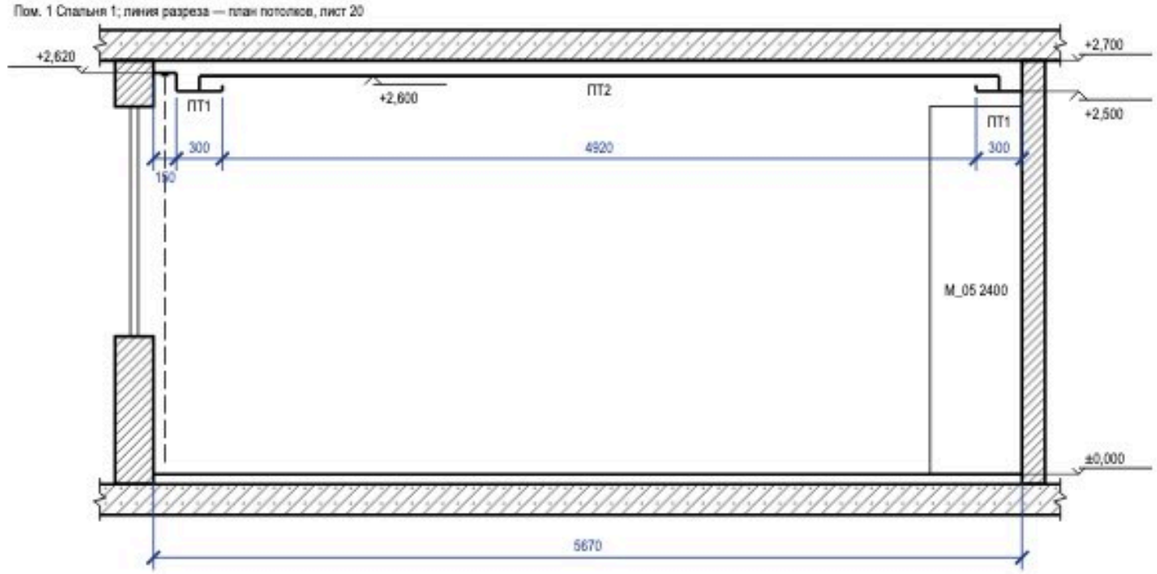

1 Короб с LED-подсветкой, теневой шов (М 1:10)


Пом. 1, 4, 6; карниз 150×100, щель под свет 60 мм

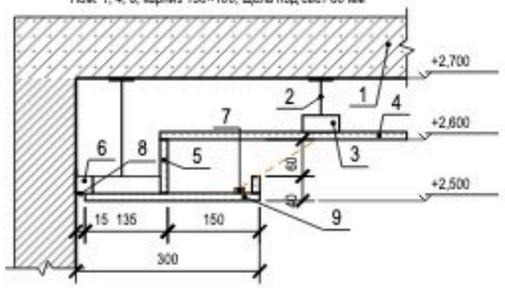

1 — плита перекрытия
2 — подвес прямой, шаг 1000 мм
3 — ПП 60×27: несущие через 500, основные через 1200 мм
4 — ГКЛ 12,5 по П113 — верхний уровень
5 — задняя стенка и бортик карниза — ГКЛ 12,5
6 — ПН 28×27 по периметру, к стене через 500 мм
7 — LED-лента в алюминиевом профиле
8 — теневой профиль: шов 15 мм, зазор 3 мм
9 — низ короба — ГКЛ 12,5 по ПП 60×27

2 Ниша под шторы (М 1:10)

Пом. 1, 4, 6; без подсветки; закладные под карниз — до обшивки

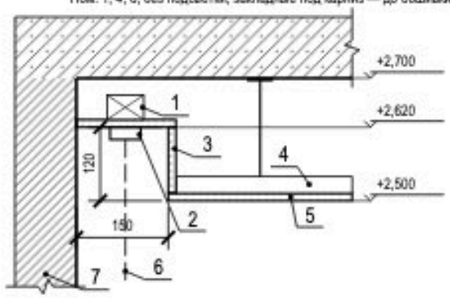

1 — закладная под карниз — брус 40×50
2 — карниз (шина), высота с верхом портьеры 100 мм
3 — стенка и потолок ниши — ГКЛ 12,5
4 — ПП 60×27 — каркас короба
5 — низ короба нижнего уровня — ГКЛ 12,5
6 — портьера
7 — стена с окном

Условные обозначения


- плита перекрытия в сечении
- стена в сечении
- потолок ГКЛ в сечении; под линией — марка потолка (план потолков)
- мебель и дверные проёмы за секущей плоскостью; число — марка и верх от чистого пола, мм
- портьера в нише под шторы

Примечания

1. Разрезы — по линиям 1–1, 2–2 на плане потолков (лист 20). Отметки — от ±0,000 чистого пола, м; размеры — мм.
2. Высоты мебели и дверных блоков за секущей плоскостью сверены с низом потолка над ними: верх ниже низа короба и поля.
3. ГКЛ 12,5 мм по каркасу П113; перепад уровней и бортик карниза — ГКЛ по ПП 60×27 (узел 1). Ниша под шторы — на всю длину стены с окном, карниз на закладной до обшивки (узел 2).
4. Толщины плит перекрытия и пирога пола показаны условно.

					Проект: Трёхкомнатная квартира			
	Лист	№ док.	Подпись	Дата	Разрезы и узлы потолков	Стадия	Лист	Листов
Дизайнер	Кырпан А.С.			05.10.26		П	21	88

выпуск 05.10.2026 № 204f23b33a · стр. 21 из 88

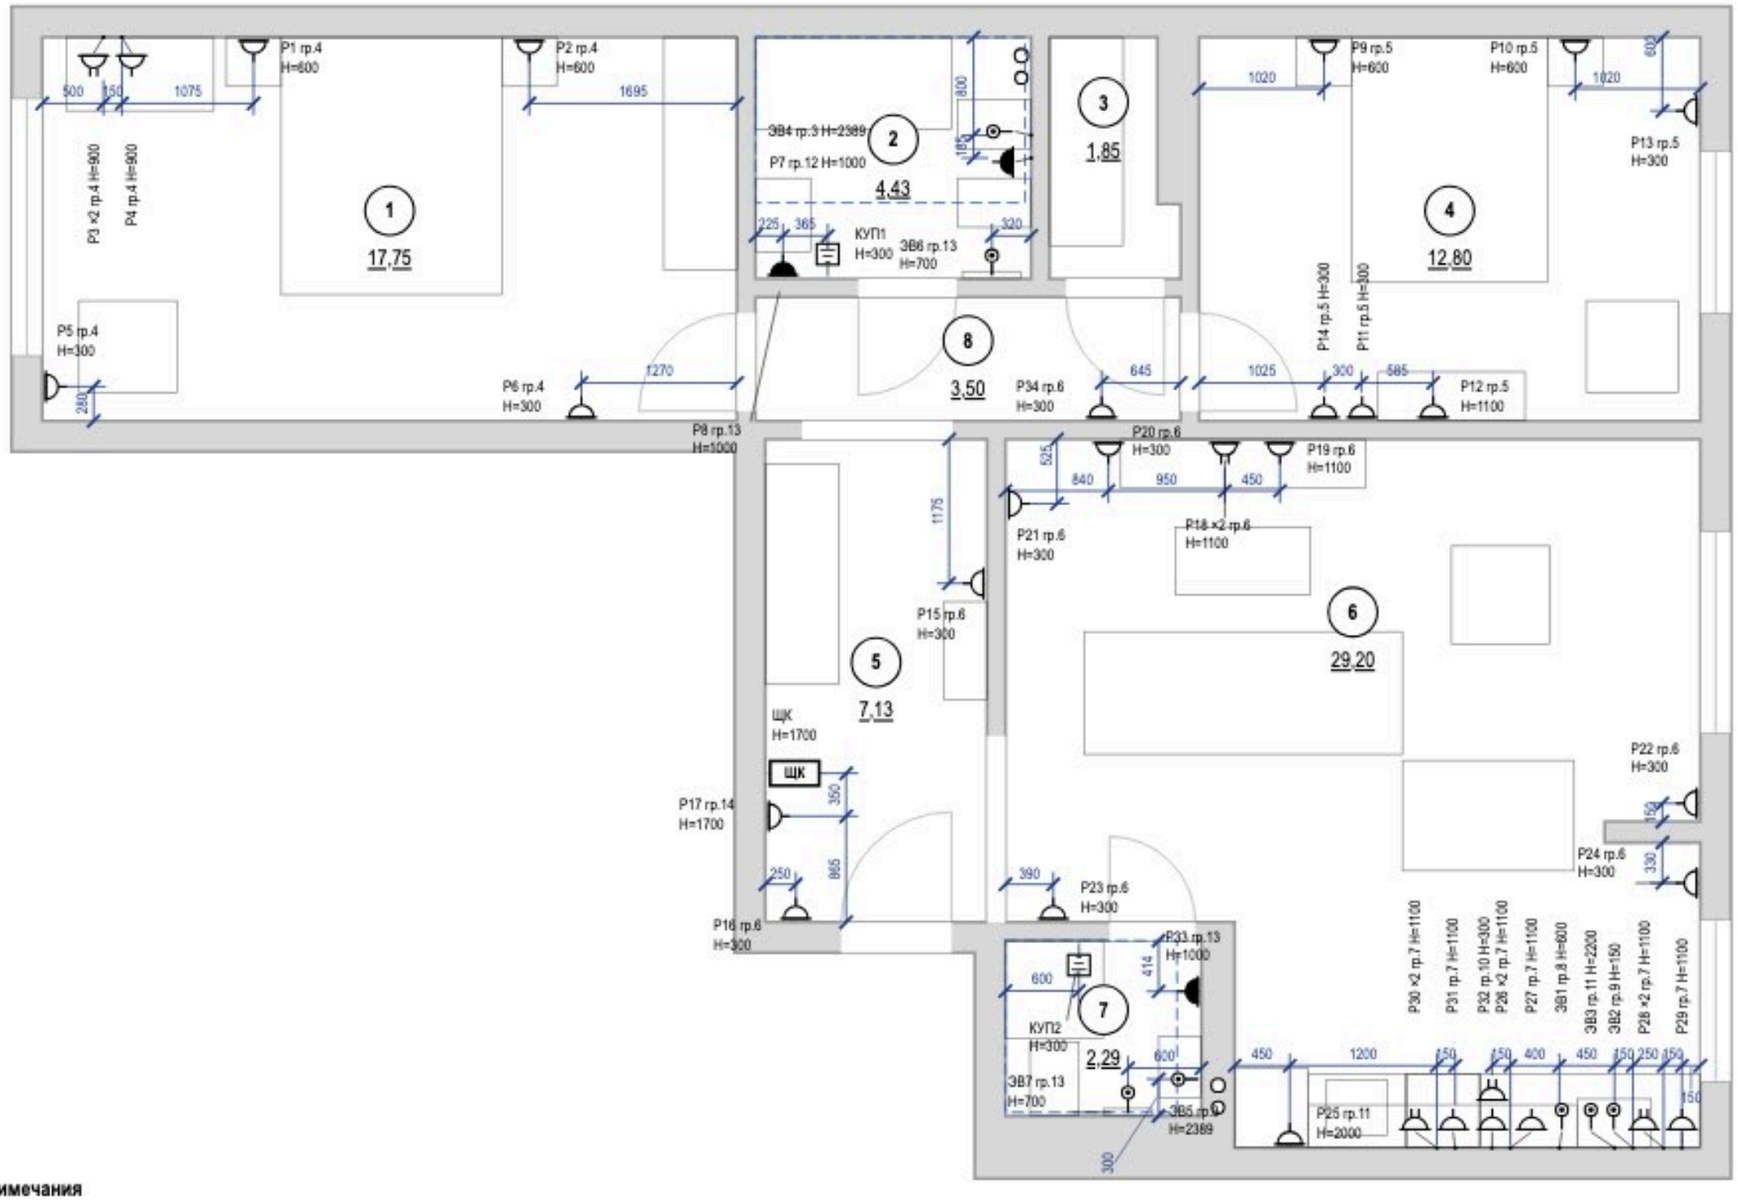

Условные обозначения

- розетка с заземляющим контактом; у знака — марка, ×N постов в рамке, гр. — группа щита, Н — высота оси, мм
- то же, рамка на 2 поста (число черточек — число постов)
- розетка влагозащищённая IP44
- вывод кабеля для подключения прибора (без розетки), марка ЭВ
- КУП — коробка уравнивания потенциалов (ДСУП), проводник к шине PE щита
- ЩК — щит квартирный
- знак разведён для читаемости: точка на стене — у выноски, привязка — до неё
- граница зоны 2 ванной (600 мм от ванны/поддона)
- мебель и сантехприборы — подложка
- стояк К1 — канализация, В1 — ХВС, Т3 — ГВС
- (1) — номер помещения, площадь м²


Примечания

1. За отметку 0,000 принят уровень чистого пола. Высоты Н — от чистого пола до оси изделия; привязки — от чистовой грани стены до оси механизма (у рамки на несколько постов — до оси рамки).
2. Высота установки, не указанная на плане: розетки — 300 мм от чистого пола; выводы кабеля — по паспорту прибора.
3. Розетки в санузле — только вне зон 0–2 (ПУЭ 7.1.48, ГОСТ Р 50571.7.701-2024), IP44, через УЗО 30 мА.
4. Розеточные и мокрые линии — через УЗО или дифавтомат с током утечки не более 30 мА (ПУЭ 7.1.79); в санузле выполнить ДСУП (ПУЭ 7.1.87–7.1.88).
5. Кабель — медный, исполнение нг(A)-LS (ГОСТ 31565-2012); скрытая прокладка только горизонтально и вертикально, фактические трассы зафиксировать исполнительной схемой до закрытия отделкой.
6. Расчёт нагрузок, токов КЗ, селективности и сечений — по проекту ЭОМ организации с допуском СРО; лист задаёт состав, расположение и группы.
7. Выводы кухонной техники — после утверждения проекта кухни (ориентировочно); привязки выводов даны от осей модулей гарнитура и пересматриваются вместе с проектом кухни.
8. Электрический тёплый пол проектом не предусмотрен; при решении заказчика устроить — отдельный лист «План тёплых полов»: контуры с отступом 100 мм от стен и мебели без ножек, датчик в гофре, терморегулятор, своя группа щита через УЗО 30 мА.
9. Ведомости электроточек, изделий, светильников и расшифровка клавиш — лист «Ведомость электроточек и изделий».

					Проект: Трёхкомнатная квартира
	Лист	№ док.	Подпись	Дата	План розеток и электровыводов
Дизайнер	Кырпан А.С.			05.10.26	

Стадия	Лист	Листов
П	22	88

выпуск 05.10.2026 · 204f23b33a · стр. 22 из 88

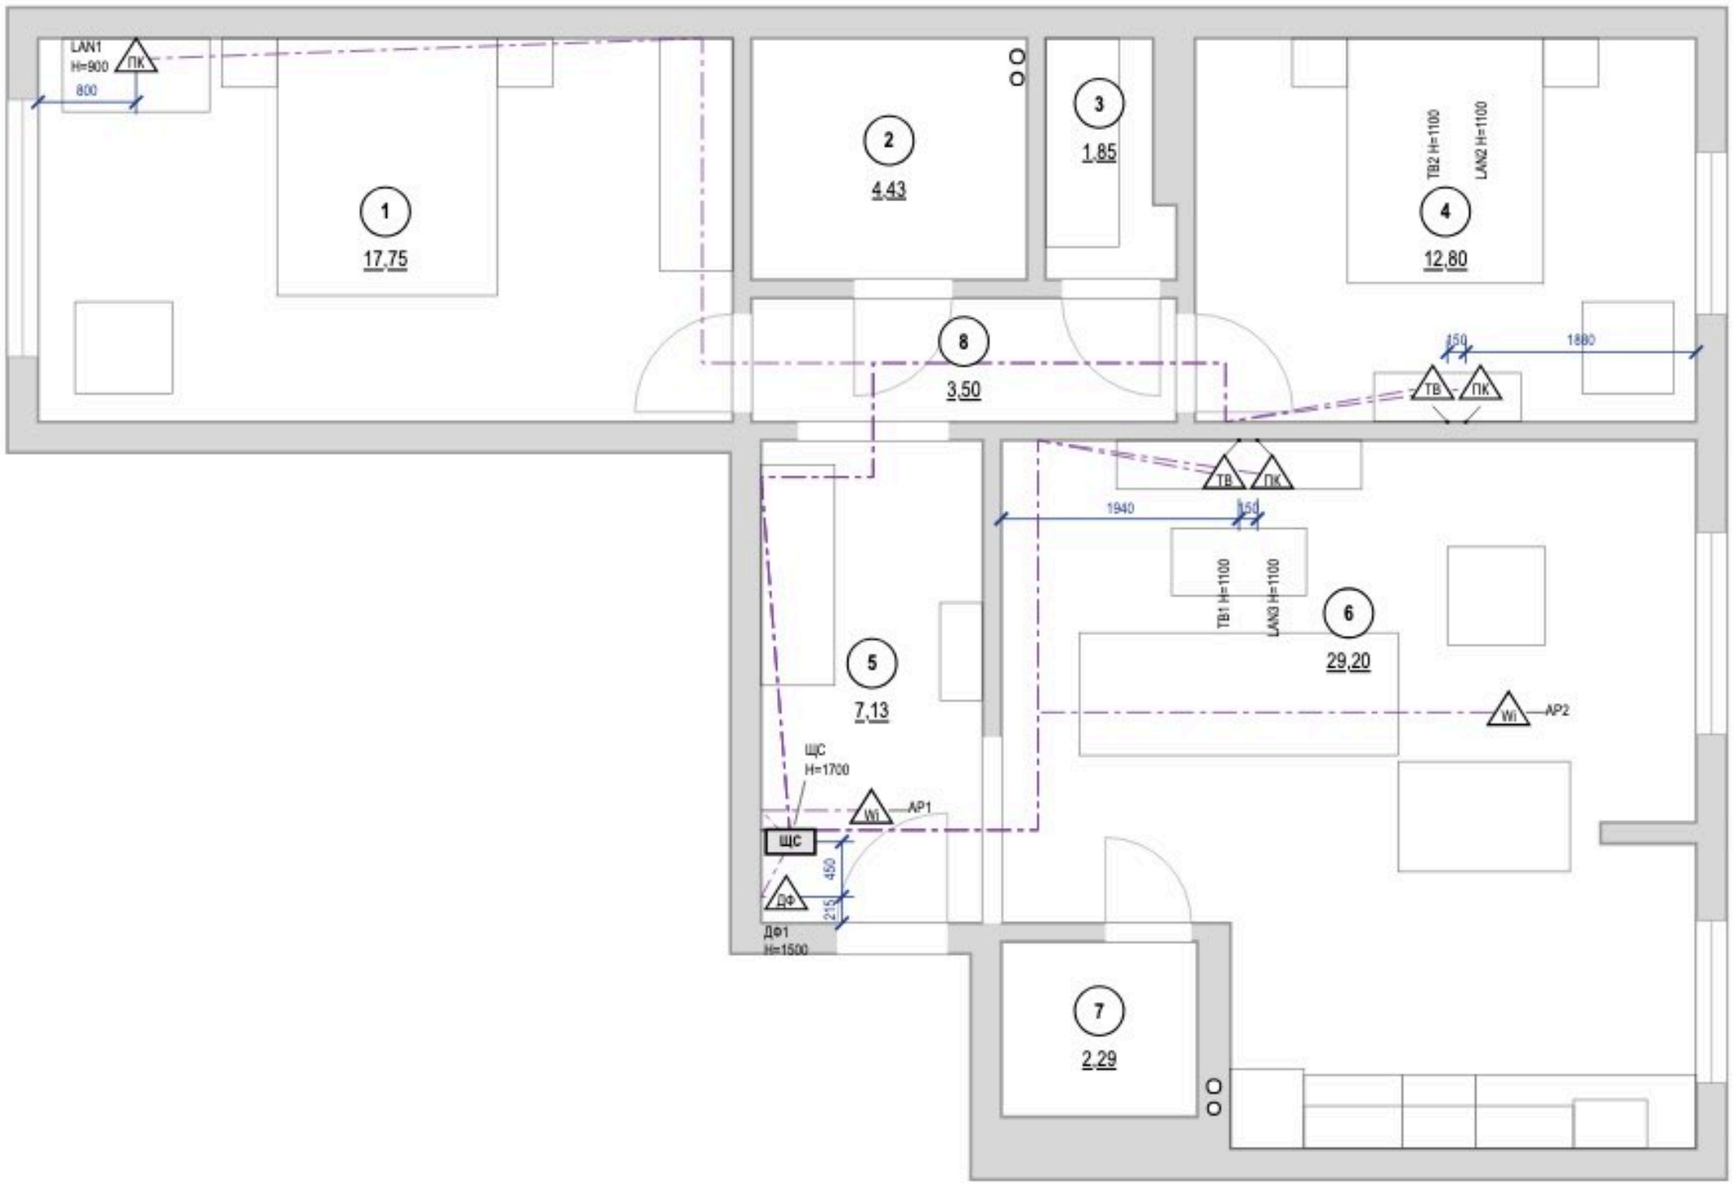


Примечания

1. За отметку 0,000 принят уровень чистого пола. Высоты Н — от чистого пола до оси изделия; привязки — от чистовой грани стены до оси механизма (у рамки на несколько постов — до оси рамки).
2. Высота установки, не указанная на плане: розетки LAN и ТВ — 300 мм от чистого пола.
3. Слаботочные кабели — отдельно от силовых: в своей трубе или лотке, при параллельной прокладке не ближе 100 мм к силовым, пересечения под прямым углом; каждую точку — отдельным кабелем от ЩС без скруток.
4. Трассы на листе — принципиальные; фактические зафиксировать исполнительной схемой до закрытия отделкой. Силовые линии, УЗО 30 мА, ДСУП, кабель нг(A)-LS — по листам розеток и щита.
5. Проект силовой части и расчёт токов КЗ — по проекту ЭОМ; слаботочная часть согласуется с провайдером и управляющей компанией (домофон, коллективное ТВ).

					Проект: Трёхкомнатная квартира
	Лист	№ док.	Подпись	Дата	
Дизайнер	Кырпан А.С.			05.10.26	План слаботочных сетей

Стадия	Лист	Листов
П	23	88

выпуск 05.10.2026 · 204f23b33a · стр. 23 из 88

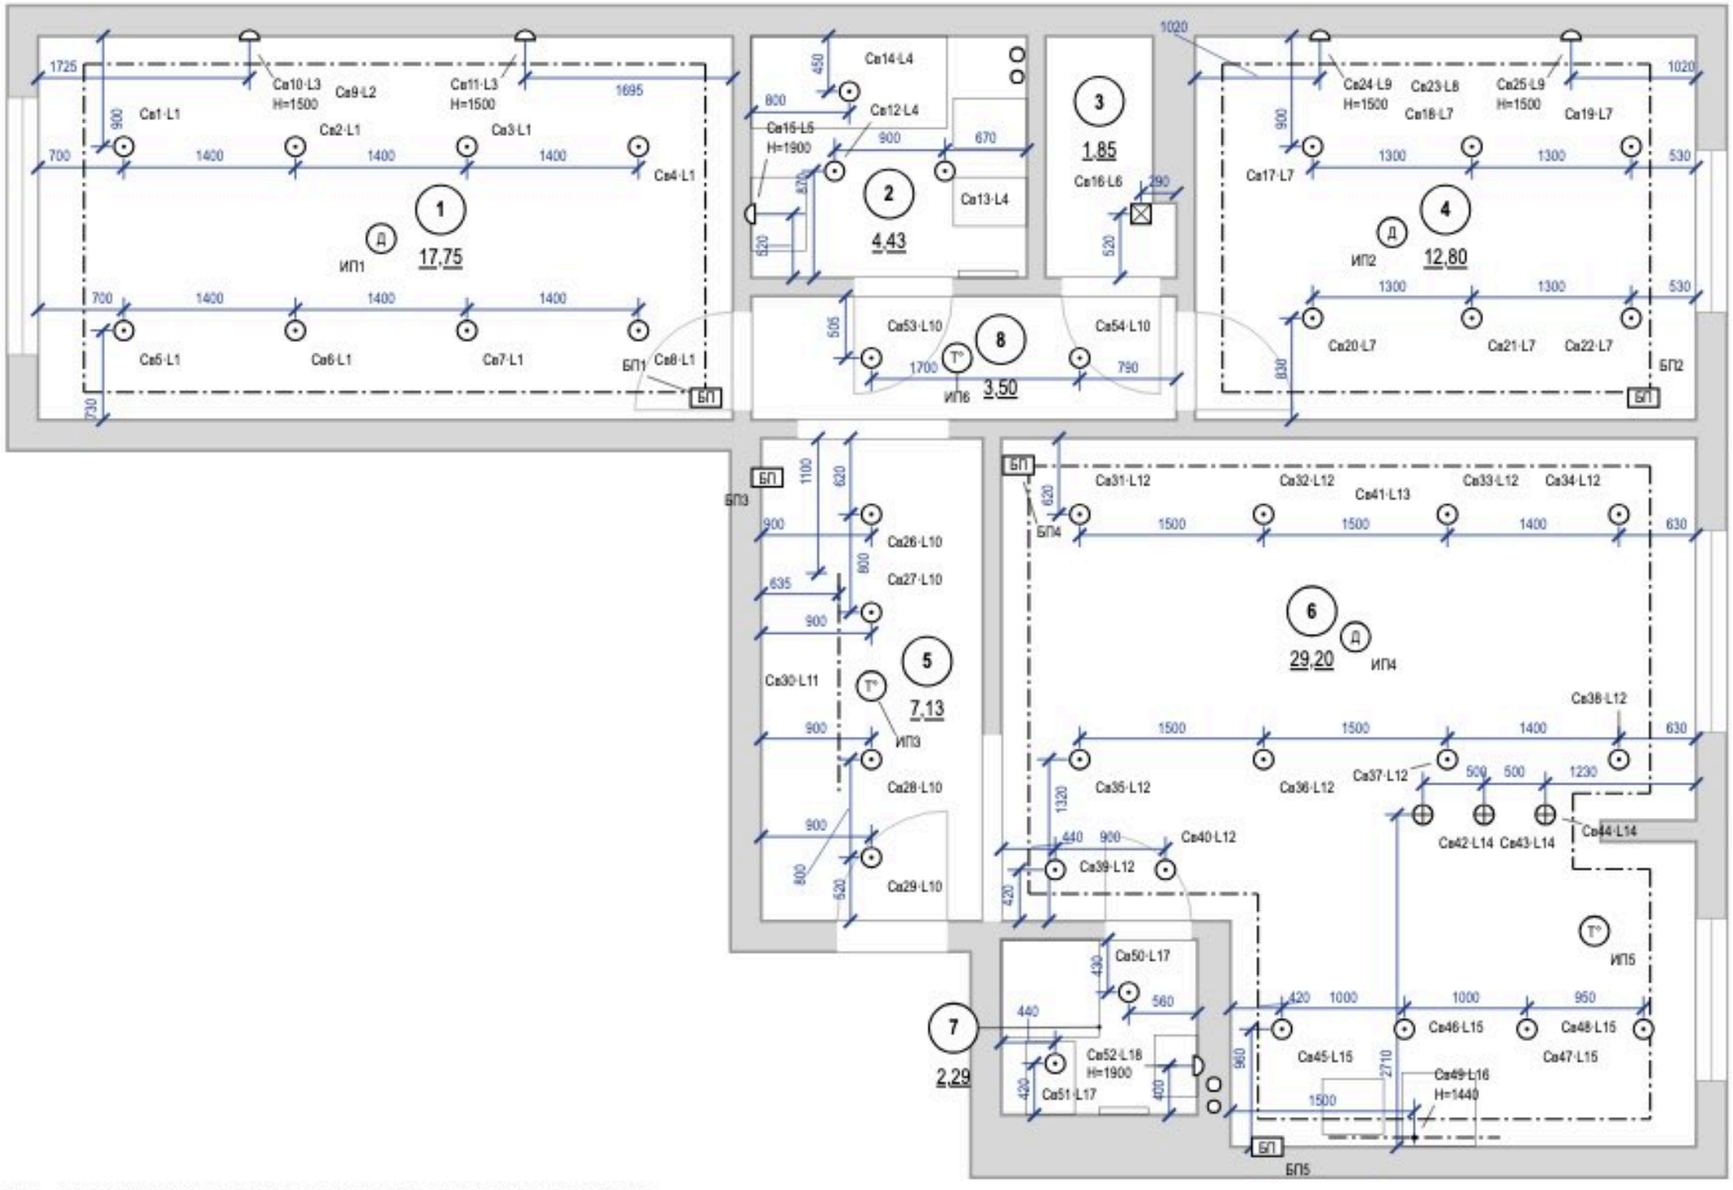

Примечания

1. За отметку 0,000 принят уровень чистого пола. Высоты H — от чистого пола до оси изделия; привязки — от чистовой грани стены до оси механизма (у рамки на несколько постов — до оси рамки).
2. Высота установки, не указанная на плане: светильники — на потолке; настенные — по отметке H у знака. Привязки — до оси светильника от чистовой грани стены, по рядам.
3. Освещённость: Eн — СанПиН 1.2.3685-21, табл. 5.52 (на полу); Φ треб. = Eн·Sk(U·MF) при U = 0,5 и MF = 0,71 (СП 52.13330.2016, табл. 4.3) — оценка, не светотехнический расчёт. Декоративная подсветка в Φ не входит.
4. Во влажных помещениях — светильники не ниже IP44; в зонах 0–2 ванной — по ГОСТ Р 50571.7.701-2024 (зона 1 — IPX5).
5. LED-лента в карнизе подсветки короба — по линии карниза с плана потолков; блок питания — в люке короба (БП на плане), питание ленты длиннее 5 м — с двух концов.
6. Розеточные и мокрые линии — через УЗО или дифавтомат с током утечки не более 30 мА (ПУЭ 7.1.79); в санузле выполнить ДСУП (ПУЭ 7.1.87–7.1.88).
7. Кабель — медный, исполнение нг(A)-LS (ГОСТ 31565-2012); скрытая прокладка только горизонтально и вертикально, фактические трассы зафиксировать исполнительной схемой до закрытия отделкой.
8. Расчёт нагрузок, токов КЗ, селективности и сечений — по проекту ЭОМ организации с допуском СРО; лист задаёт состав, расположение и группы.
9. Ведомость светильников — лист «Ведомость электроточек и изделий».

					Проект: Трёхкомнатная квартира
	Лист	№ док.	Подпись	Дата	
Дизайнер	Кырпан А.С.			05.10.26	План освещения

Стадия	Лист	Листов
П	24	88

выпуск 05.10.2026 № 204f23b33a · стр. 24 из 88

Спецификация светильников

Поз.	Марки	Наименование	Установка	Кол.	P, Вт	Σ P, Вт	Ф, лм	Tц, K	Ra	Угол, °	IP	Дим.	Группа	Пом.
1	Св1–Св8	Встраиваемый точечный	в ГКЛ, корпус ≤ 70 мм	8	12	96	1000	2700	90	—	20	—	L1	1
2	Св9	Лента светодиодная 24 В	в карнизе короба, профиль с рассеивателем	15,5 м	9,6/м	148,8	900/м	2700	90	—	20	да	L2	1
3	Св10, Св11, Св24, Св25	Настенный (бра)	на стене, H=1500	4	6	24	400	2700	90	60	20	—	L3, L9	1, 4
4	Св12–Св14, Св51	Встраиваемый точечный	в ГКЛ, корпус ≤ 70 мм	4	6	24	500	3000	90	—	44	—	L4, L17	2, 7
5	Св15, Св52	Настенный светильник над зеркалом, драйвер встроен	над зеркалом, H=1900	2	8	16	600	3000	90	—	44	—	L5, L18	2, 7
6	Св16	Потолочный накладной	на потолке, засветка стены	1	10	10	900	3000	90	—	20	—	L6	3
7	Св17–Св22	Встраиваемый точечный	в ГКЛ, корпус ≤ 70 мм	6	12	72	1050	2700	90	—	20	—	L7	4
8	Св23	Лента светодиодная 24 В	в карнизе короба, профиль с рассеивателем	12,3 м	9,6/м	118,5	900/м	2700	90	—	20	да	L8	4
9	Св26–Св29, Св53, Св54	Встраиваемый точечный	в ГКЛ, корпус ≤ 70 мм	6	7	42	600	3000	90	—	20	—	L10	5, 8
10	Св30	Лента светодиодная 24 В	в коробе, профиль с рассеивателем, датчик движения	1,8 м	4,8/м	8,6	150/м	2700	90	—	20	нет	L11	5
11	Св31–Св40	Встраиваемый точечный	в ГКЛ, корпус ≤ 70 мм	10	12	120	1000	3000	90	—	20	да	L12	6
12	Св41	Лента светодиодная 24 В	в карнизе короба, профиль с рассеивателем	22,1 м	9,6/м	211,8	900/м	2700	90	—	20	да	L13	6
13	Св42, Св43, Св44	Подвесной	подвес, низ H=1450	3	9	27	800	3000	90	—	20	да	L14	6
14	Св45–Св48	Встраиваемый точечный	в ГКЛ, корпус ≤ 70 мм	4	10	40	900	3000	90	—	20	да	L15	6
15	Св49	Линейный настенный	под верхними шкафами, H=1440	1	18	18	1500	3000	90	—	20	да	L16	6
16	Св50	Встраиваемый точечный	в ГКЛ, корпус ≤ 70 мм	1	7	7	600	3000	90	—	44	—	L17	7
		Итого		**50 шт + 51,7 м**		**983,7**								

Слои света по помещениям

Пом.	Помещение	Слои света и группы включения (марки светильников)	Tц, K	Ra	Σ P, Вт	Сцен.
1	Спальня 1	общий — L1 (Св1–Св8); рабочий — L3 (Св10, Св11); акцентный — L2 (Св9)	2700	90	256,8	2
2	Ванная	общий — L4 (Св12–Св14); рабочий — L5 (Св15)	3000	90	26	—
3	Гардеробная	общий — L6 (Св16)	3000	90	10	—
4	Спальня 2	общий — L7 (Св17–Св22); рабочий — L9 (Св24, Св25); акцентный — L8 (Св23)	2700	90	202,5	1
5	Прихожая	общий — L10 (Св26–Св29); ночной — L11 (Св30)	2700 / 3000	90	36,6	—
6	Кухня-гостиная	общий — L12 (Св31–Св40), L14 (Св42, Св43, Св44), L15 (Св45–Св48); рабочий — L16 (Св49); акцентный — L13 (Св41)	2700 / 3000	90	416,8	4
7	Санузел 2	общий — L17 (Св50, Св51); рабочий — L18 (Св52)	3000	90	21	—
8	Коридор	общий — L10 (Св53, Св54)	3000	90	14	—

LED-ленты, линейные светильники и блоки питания

Марка	Пом.	L, м	U, В	Вт/м	Σ P, Вт	БП	P БП, Вт	Загр., %	Питание	Доступ к БП
Св9	1	15,5	24	9,6	148,8	БП1	200	74	с двух концов	люк 300×300 в коробе У1 у входа
Св23	4	12,3	24	9,6	118,5	БП2	200	59	с двух концов	люк 300×300 в коробе У1 у окна
Св30	5	1,8	24	4,8	8,6	БП3	20	43	с одного конца	в шкафу M_13, верхняя полка
Св41	6	22,1	24	9,6	211,8	БП4	300	71	с двух концов	люк 300×300 в коробе У1 у входа
Св49	6	3	24	—	18	БП5	60	30	встроенный ввод	в пенале M_19, верх, съёмная панель

Сценарии освещения

Пом.	Сценарий	Группы и уровни, %	Чем включается
1	Вечер	L1 споты — 0; L2 подсветка короба — 100; L3 бра — 100	S1, S2, S3
1	Уборка	L1 споты — 100; L2 подсветка короба — 100; L3 бра — 0	S1, S2, S3
4	Вечер	L7 споты — 0; L8 подсветка короба — 100; L9 бра — 100	S4, S5, S6
6	Вечер	L12 споты гостиной — 30; L13 подсветка короба — 100; L14 подвесы над столом — 50; L15 споты кухни — 0; L16 подсветка столешницы — 0	S10 светорегулятор, S11 светорегулятор
6	Ужин	L12 споты гостиной — 0; L13 подсветка короба — 60; L14 подвесы над столом — 100; L15 споты кухни — 0; L16 подсветка столешницы — 30	S10 светорегулятор, S11 светорегулятор, S12 светорегулятор
6	Кино	L12 споты гостиной — 0; L13 подсветка короба — 20; L14 подвесы над столом — 0; L15 споты кухни — 0; L16 подсветка столешницы — 0	S10 светорегулятор
6	Готовка	L12 споты гостиной — 50; L13 подсветка короба — 0; L14 подвесы над столом — 0; L15 споты кухни — 100; L16 подсветка столешницы — 100	S10 светорегулятор, S11 светорегулятор, S12 светорегулятор
все	Ушёл	все группы — 0 (свет выключен)	выключатели помещений

Слои света

общий — равномерный свет помещения, по норме освещённости

рабочий — местный свет задачи: столешница, зеркало, чтение у кровати

акцентный — подсветка потолка, стен и ниш; не входит в поток общего света


ночной — путь спальня → санузел: не выше 2700 K, малая яркость, датчик движения

Примечания

1. Позиции и марки Св — те же, что на плане освещения (лист 24) и в ведомости светильников (лист «Ведомость электроточек и изделий»); группы L — по плану выключателей (лист 26).
2. Модели светильников не назначены: подбор по графам спецификации — поток, Tц, Ra, угол, IP и диммирование не хуже указанных, мощность не больше; встраиваемые — под глубину короба (графа «Установка»). IP 20 — сухие помещения.
3. Длина LED-ленты в карнизе — по линии карниза плана потолков (лист 20); Σ P = Вт/м × длина. Блок питания загружен не больше чем на 80 %; лента 24 В длиннее 10 м питается с двух концов; доступ к блоку питания — люк ревизии 300×300 мм или место, указанное в таблице.
4. Сценарии: уровень — доля максимальной яркости группы, %; 0 — группа выключена. Уровень ниже 100 % — только у групп на светорегуляторе (задний фронт, TE) с диммируемыми драйверами и блоками питания.
5. Мощность и поток — по паспортам принятых изделий, Σ P — установленная мощность освещения. Оценка освещённости — на плане освещения; это не светотехнический расчёт.

					Проект: Трёхкомнатная квартира			
	Лист	№ док.	Подпись	Дата	Спецификация светильников и сценарии освещения	Стадия	Лист	Листов
Дизайнер	Кырпан А.С.			05.10.26		П	25	88

выпуск 05.10.2026 № 204f23b33a · стр. 25 из 88

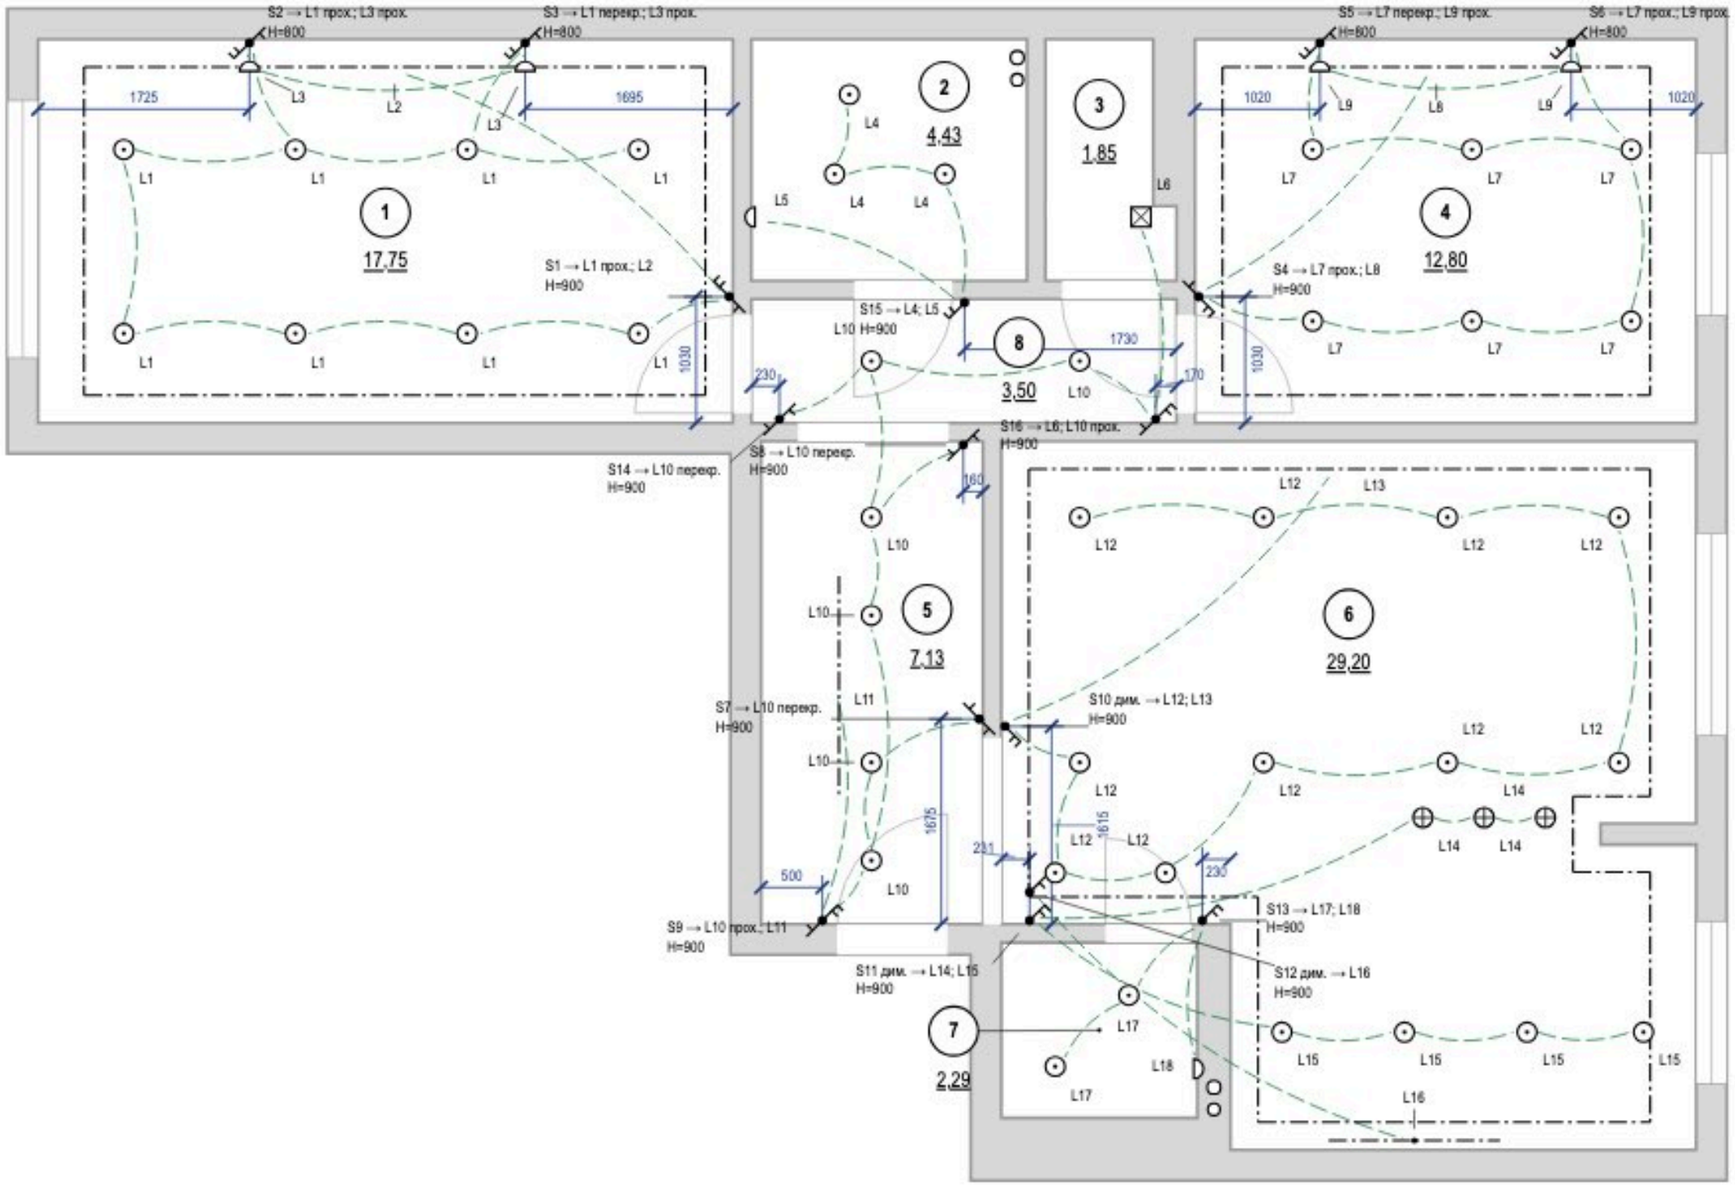


Примечания

1. За отметку 0,000 принят уровень чистого пола. Высоты H — от чистого пола до оси изделия; привязки — от чистовой грани стены до оси механизма (у рамки на несколько постов — до оси рамки).
2. Высота установки, не указанная на плане: выключатели — 900 мм от чистого пола, со стороны дверной ручки (ПУЭ 7.1.51).
3. Линии связи показывают, какой выключатель какую группу L включает; это не трасса кабеля. Трасса — принципиальная, фактическую зафиксировать исполнительной схемой.
4. Группы из нескольких мест (L1 — S1, S2, S3; L3 — S2, S3; L7 — S4, S5, S6; L9 — S5, S6; L10 — S7, S8, S9, S14, S16): на крайних местах — проходные клавиши, на промежуточных — перекрёстные; механизмы — в ведомости изделий.
5. Светорегулятор — по заднему фронту (для LED-драйверов), совместимость с драйверами проверить до закупки.
6. Розеточные и мокрые линии — через УЗО или дифавтомат с током утечки не более 30 мА (ПУЭ 7.1.79); в санузле выполнить ДСУП (ПУЭ 7.1.87–7.1.88).
7. Кабель — медный, исполнение нг(A)-LS (ГОСТ 31565-2012); скрытая прокладка только горизонтально и вертикально, фактические трассы зафиксировать исполнительной схемой до закрытия отделкой.
8. Расчёт нагрузок, токов КЗ, селективности и сечений — по проекту ЭОМ организации с допуском СРО; лист задаёт состав, расположение и группы.
9. Расшифровка клавиш и ведомость изделий — лист «Ведомость электроточек и изделий».

					Проект: Трёхкомнатная квартира	
	Лист	№ док.	Подпись	Дата		
Дизайнер	Кырпан А.С.			05.10.26	Управление светильниками	Стадия: П; Лист: 26; Листов: 88

выпуск 05.10.2026 · 204f23b33a · стр. 26 из 88

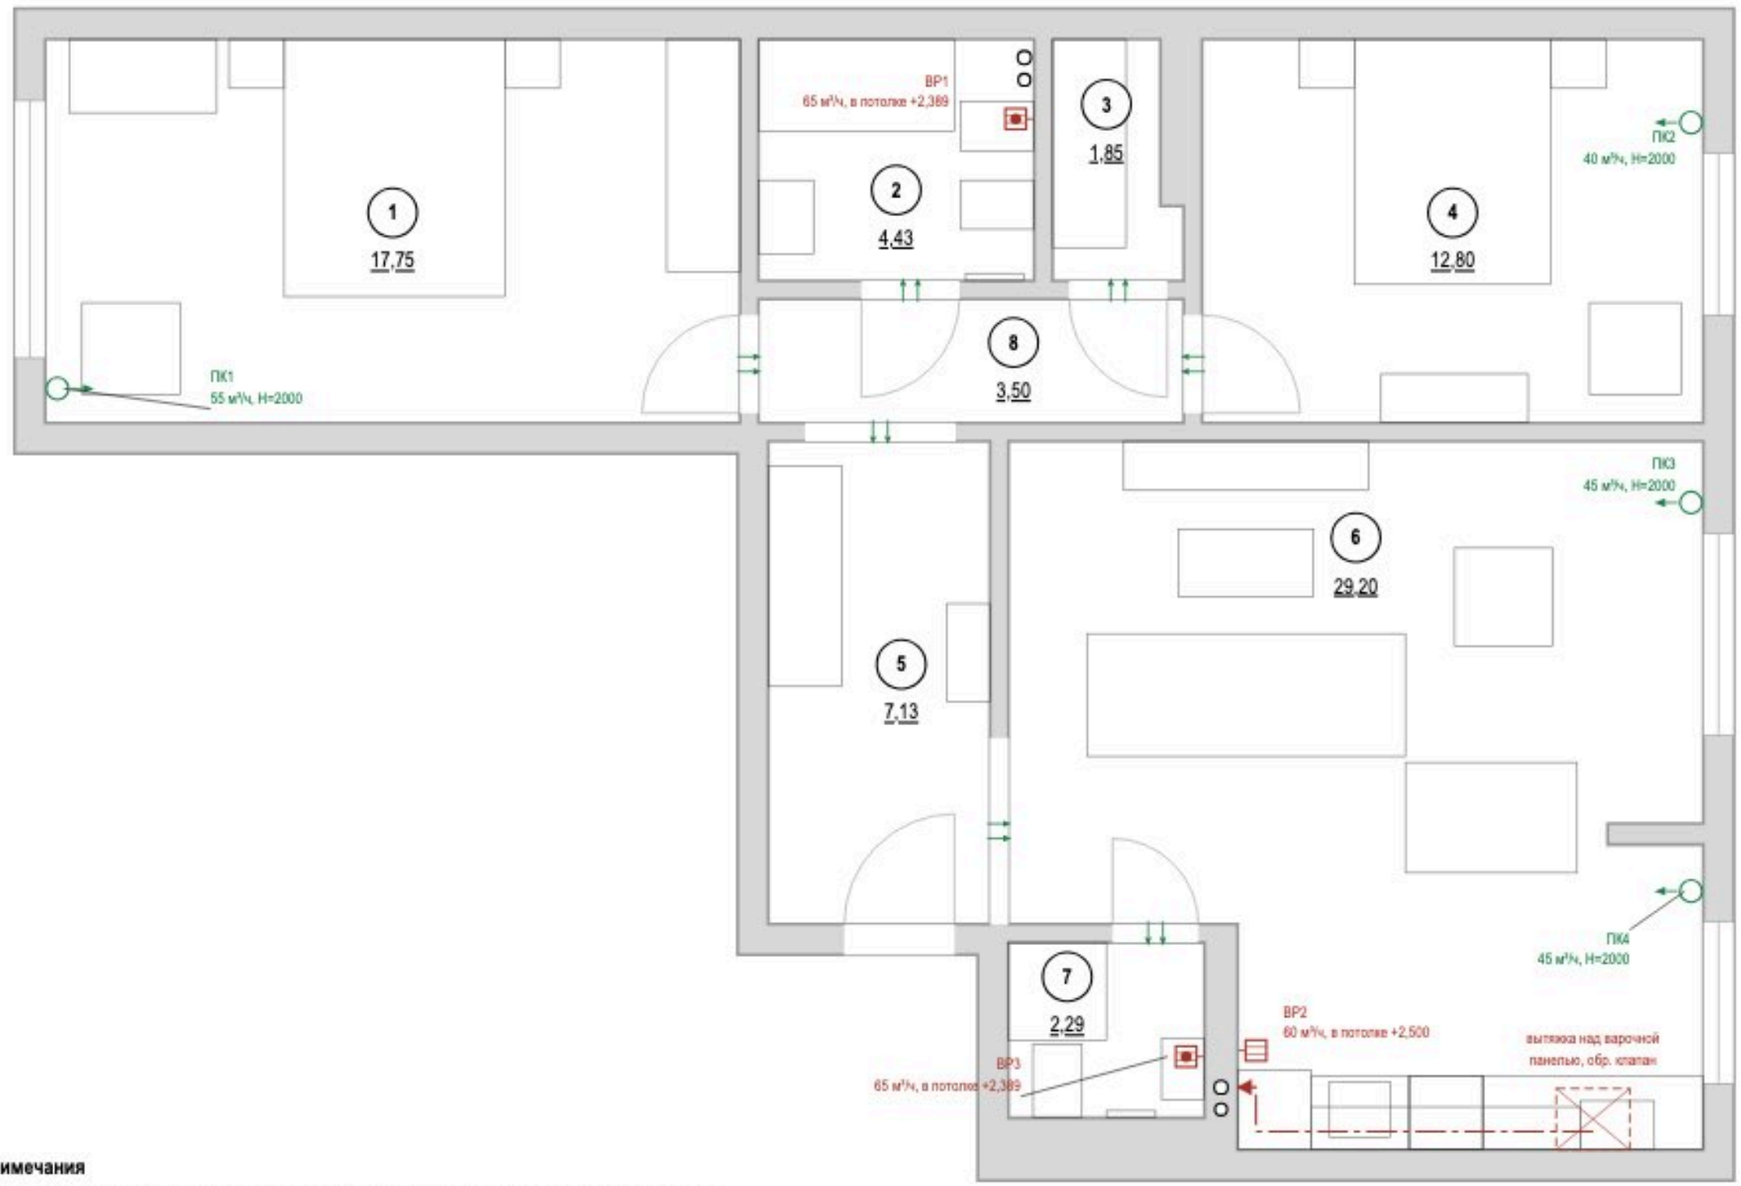

Условные обозначения

- стояк: К1 — канализация, В1 — ХВС, Т3 — ГВС
- номер помещения, площадь м²
- вытяжная решётка в подшивном потолке, воздуховод за потолком до канала
- вентилятор с обратным клапаном в подшивном потолке, воздуховод за потолком до канала
- приточный клапан (КИВ) в наружной стене: марка, расход, Н центра
- переток: зазор под полотном или переточная решётка
- кухонная вытяжка над варочной панелью
- воздуховод кухонной вытяжки в коробе под потолком
- отдельный вход воздуховода в вентканал, обратный клапан

Воздухообмен, м³/ч

№	Помещение	Выт. норма	Выт. проект	Прит. норма	Прит. проект	Устройства
1	Спальня 1			54	55	ПК1
2	Ванная	50	65			ВР1
3	Гардеробная	1				переток
4	Спальня 2			39	40	ПК2
6	Кухня-гостиная	60	60	88	90	ВР2, ПК3, ПК4
7	Санузел 2	50	65			ВР3
	Итого	**161**	**190**	**181**	**185**	

Воздухообмен квартиры — по большей из сумм притока и вытяжки: норма 181 м³/ч, проект 190 м³/ч.
Вытяжка не меньше притока — баланс сведён.

Привязки — до обмера
Вентканалы в исходных данных не заданы: решётки и вход вытяжки показаны у стояков К1 (вентблок у мокрой зоны). До черновых работ — обмер каналов и проверка тяги; лист перевыпустить по факту.

Примечания

1. Расчёт систем ОВ и подбор оборудования — проектная организация с допуском СРО; лист даёт места, трассы и привязки.
2. Нормы вытяжки — СП 54.13330.2022 (Изм. 1, 2), табл. 7.1: кухня с электроплитой 60 м³/ч, с газовой 100; ванная и совмещённый санузел 50; уборная 25; гардеробная 0,2 ч⁻¹. Приток в жилые — 3 м³/ч на 1 м² (менее 20 м² общей площади на человека), иначе 30 м³/ч на человека.
3. Вентканалы и шахты не сужать, не переносить и не закрывать; вентилятор и кухонная вытяжка — через обратный клапан, без перекрытия естественной тяги.
4. Проектные расходы — не ниже нормы, вытяжка сведена с притоком вентиляторами мокрых помещений. Клапаны — в простенке у окна, центр 2000 мм, не над кроватью, не ближе 300 мм к стоякам отопления; типоразмер — на расход.
5. Под подшивным потолком вытяжка — в потолке, воздуховодом за потолком до канала. Кухонная вытяжка в воздухообмен не включена: воздуховод не менее Ø125 в коробе, вход в канал отдельный.
6. Переток — зазор под полотнами межкомнатных дверей или переточная решётка.
7. Кондиционирование заданием не предусмотрено; при установке трассы фреона и дренажа (не менее 40 мм/м, в К1 через сифон) и питание заложить до черновых работ.
8. Привязки оборудования — по паспортам приобретённых моделей, до черновых работ.

	Лист	№ док.	Подпись	Дата
Дизайнер	Кырпан А.С.			05.10.26

Проект: Трёхкомнатная квартира

План вентиляции

Стадия	Лист	Листов
П	27	88

выпуск 05.10.2026 · 204f23b33a · стр. 27 из 88



Условные обозначения

- (1) — номер помещения, площадь м²
- радиатор отопления (марка РО-N, длина по плану)
- клапан с термоголовкой на подаче
- стояк отопления, подающий (Ст Т1-N)
- стояк отопления, обратный (Ст Т2-N)
- Т1 — отопление, подающий трубопровод
- Т2 — отопление, обратный трубопровод

Ведомость радиаторов

Марка	Помещение	Тип	Д×В×Г, мм	Низ / стена	Q, Вт
РО-1	1. Спальня 1	панельный	1400×600×100	120 / 40	расч.
РО-2	4. Спальня 2	панельный	900×600×100	120 / 40	расч.
РО-3	6. Кухня-гостиная	панельный	1100×600×100	120 / 40	расч.
РО-4	6. Кухня-гостиная	панельный	900×600×100	120 / 40	расч.

тип и мощность — по теплотехническому расчёту
Низ — от чистого пола, стена — зазор до задней панели, мм.

Привязки — до обмера
Стояки отопления в исходных данных не заданы: показаны у откосов окон, подводки — принципиально. До черновых работ — обмер стояков и паспорта приборов; лист перевыпустить по факту.


Примечания

1. Расчёт системы отопления, теплопотерь и подбор приборов — проектная организация с допуском СРО; лист даёт места и привязки.
2. Тип, длина и мощность радиаторов — по теплотехническому расчёту; лист задаёт места, зазоры и подключение.
3. Радиаторы — под каждым окном жилых комнат и кухни, центр по оси проёма, длина 0,7 ширины окна (кратно 100); окончательно — по расчёту.
4. Зазоры радиатора: низ не менее 100 мм от чистого пола, верх не менее 100 мм до подоконника, 30–50 мм от стены до задней панели; центр по оси окна с допуском ±20 мм.
5. Радиаторы не закрывать глухими коробами и мебелью; перенос и замена приборов в многоквартирном доме — переустройство, согласование с управляющей организацией (ЖК РФ ст. 25–26); вынос на лоджию запрещён.
6. Трубы отопления через межквартирные стены не прокладывать (СП 51.13330.2011, п. 9.19); через перекрытия и перегородки — в гильзах.
7. Привязки приборов и подводок — по паспортам приобретённых радиаторов и клапанов, до черновых работ.
8. До закрытия отделкой трубопроводы отопления испытать гидростатическим давлением с оформлением акта (СП 73.13330.2016, 7.2–7.3).

					Проект: Трёхкомнатная квартира
	Лист	№ док.	Подпись	Дата	План отопления
Дизайнер	Кырпан А.С.			05.10.26	

Стадия	Лист	Листов
П	28	88

выпуск 05.10.2026 № 204f23b33a · стр. 28 из 88

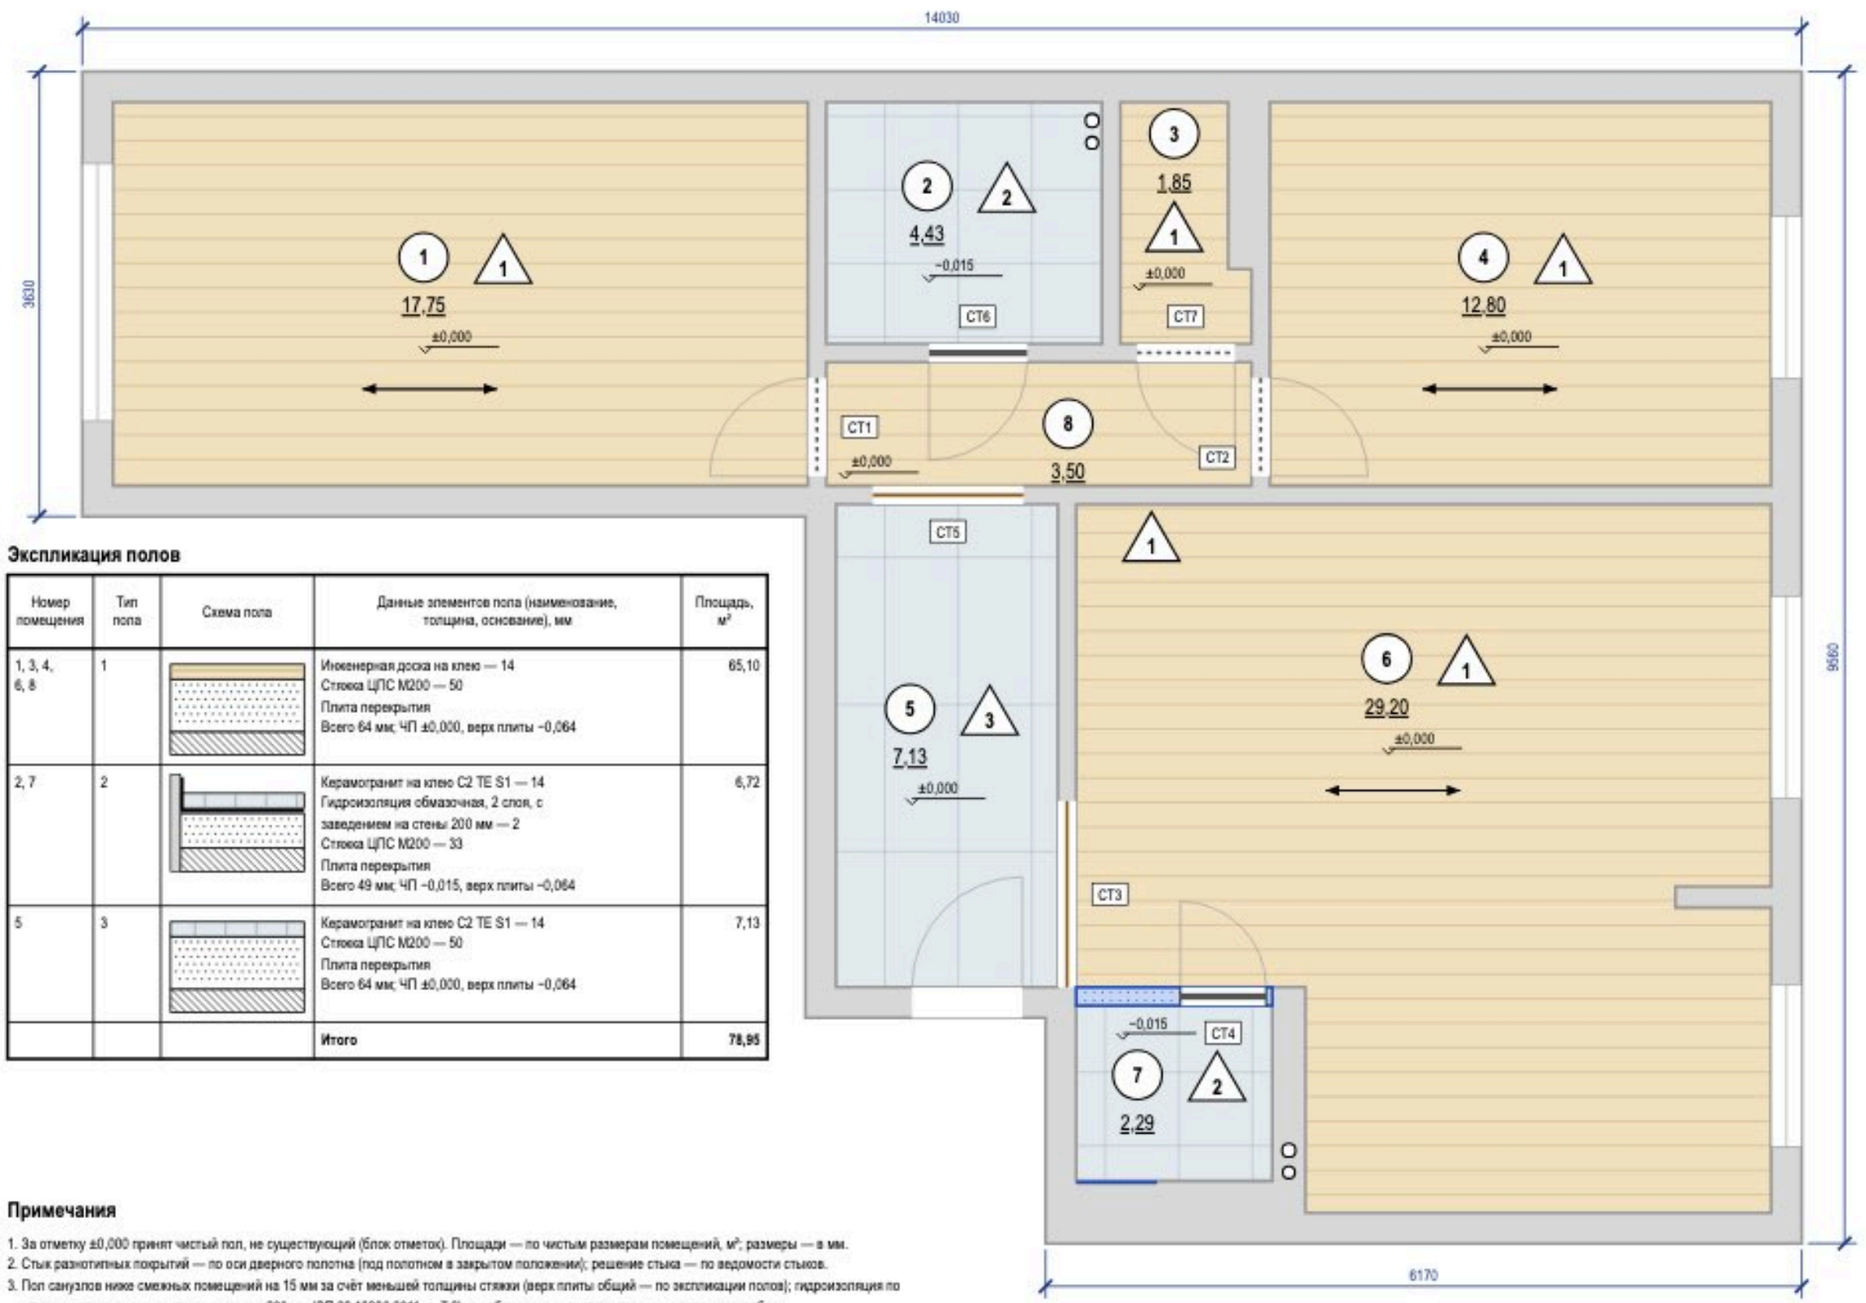

Спецификация плинтусов

Наименование	Помещения	Длина, м (с запасом)
Плинтус МДФ под покраску 80×16, крепление к стене, окраска в цвет Farrow & Ball No. 241	1, 3, 4, 5, 6, 8	78

Отметки по высоте

±0,000	чистый пол пом. 1, 3–6, 8; отсчёт высот
−0,015	чистый пол пом. 2, 7, ниже на 15 мм
−0,064	верх плиты — расчёт, не замер
сущ. пол	снимается до плиты; не замерен

Экспликация полов

Номер помещения	Тип пола	Схема пола	Данные элементов пола (наименование, толщина, основание), мм	Площадь, м²
1, 3, 4, 6, 8	1		Инженерная доска на клею — 14 Стяжка ЦПС М200 — 50 Плита перекрытия Всего 64 мм; ЧП ±0,000, верх плиты −0,064	65,10
2, 7	2		Керамогранит на клею C2 TE S1 — 14 Гидроизоляция обмазочная, 2 слоя, с заведением на стены 200 мм — 2 Стяжка ЦПС М200 — 33 Плита перекрытия Всего 49 мм; ЧП −0,015, верх плиты −0,064	6,72
5	3		Керамогранит на клею C2 TE S1 — 14 Стяжка ЦПС М200 — 50 Плита перекрытия Всего 64 мм; ЧП ±0,000, верх плиты −0,064	7,13
			Итого	**78,95**

Примечания


1. За отметку ±0,000 принят чистый пол, не существующий (блок отметок). Площади — по чистым размерам помещений, м²; размеры — в мм.
2. Стык разнотипных покрытий — по оси дверного полотна (под полотном в закрытом положении); решение стыка — по ведомости стыков.
3. Пол санузлов ниже смежных помещений на 15 мм за счёт меньшей толщины стяжки (верх плиты общий — по экспликации полов); гидроизоляция по стяжке с заведением на стены не менее 200 мм (СП 29.13330.2011, п. 7.2), до облицовки — тест проливом и акт скрытых работ.
4. Трубопроводы в конструкции пола не прокладываются: пирог пола 49–64 мм не вмещает выпуски канализации с уклоном — выпуски К1 ведутся по стенам над чистым полом в коробах (лист 15).
5. Звукоизоляционный слой под стяжкой проектом не предусмотрен (стяжка по плите): приведённый уровень ударного шума перекрытия с полом L_{nw} не более 60 дБ (СП 51.13330.2011, табл. 2) подтвердить по данным дома; при превышении — плавающая стяжка по звукоизоляции с демпферной лентой по контуру и у стояков, пирог пересчитать.
6. Штучные покрытия (инженерная доска): направление — по стрелке; влажность основания по СМ не более 2,0 % (по ТУ изготовителя).
7. Ровность основания — просвет под 2-метровой рейкой не более 2 мм: пом. 1, 3, 4, 6, 8 (инженерная доска), пом. 2, 5, 7 (керамогранит); проверить до укладки покрытия (СП 71.13330.2017, табл. 8.5).
8. Сетка на плитке — условная, в размер формата; точка старта и раскладка — по листу раскладки плитки.
9. Пироги полов — по экспликации полов: слои сверху вниз, толщины в мм; гидроизоляция мокрых зон — в пироге и в ведомости отделки; схема пола — без масштаба.

					Проект: Трёхкомнатная квартира
	Лист	№ док.	Подпись	Дата	План покрытий пола
Дизайнер	Кырпан А.С.			05.10.26	


Стадия	Лист	Листов
П	29	88

выпуск 05.10.2026 · 204f23b33a · стр. 29 из 88

Фрагмент 1. Ванная (пом. 2). Пол 600×600, шов 2 мм, М 1:20

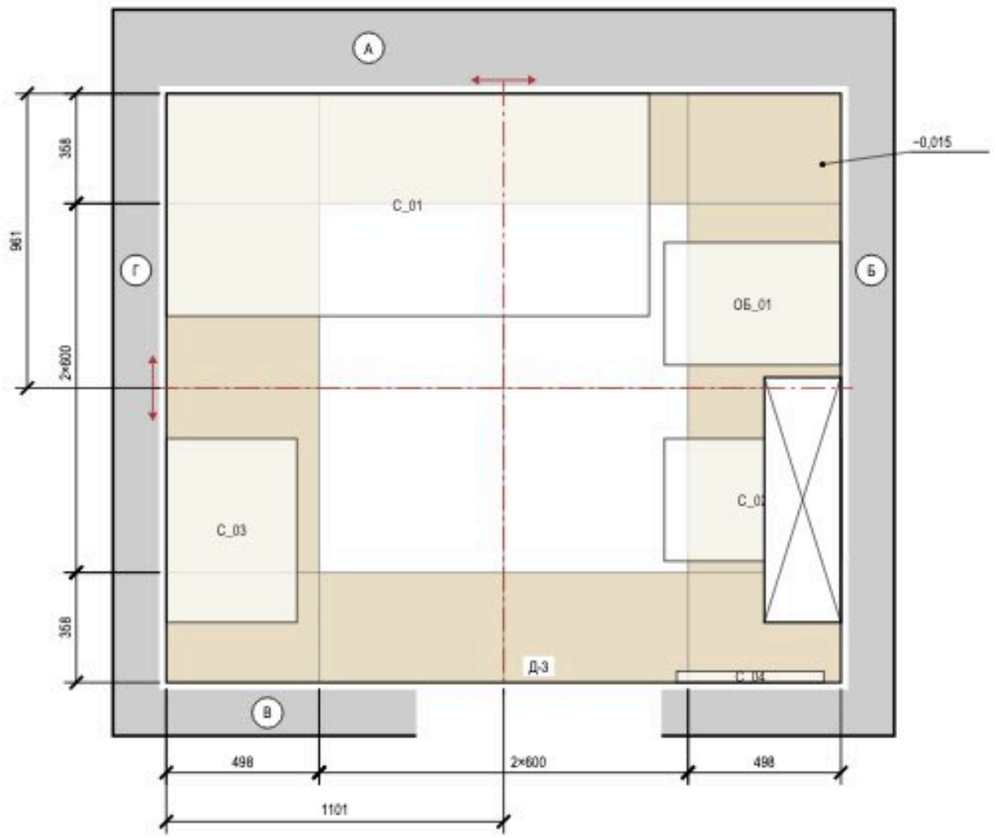

Фрагмент 2. Санузел 2 (пом. 7). Пол 600×600, шов 2 мм, М 1:20

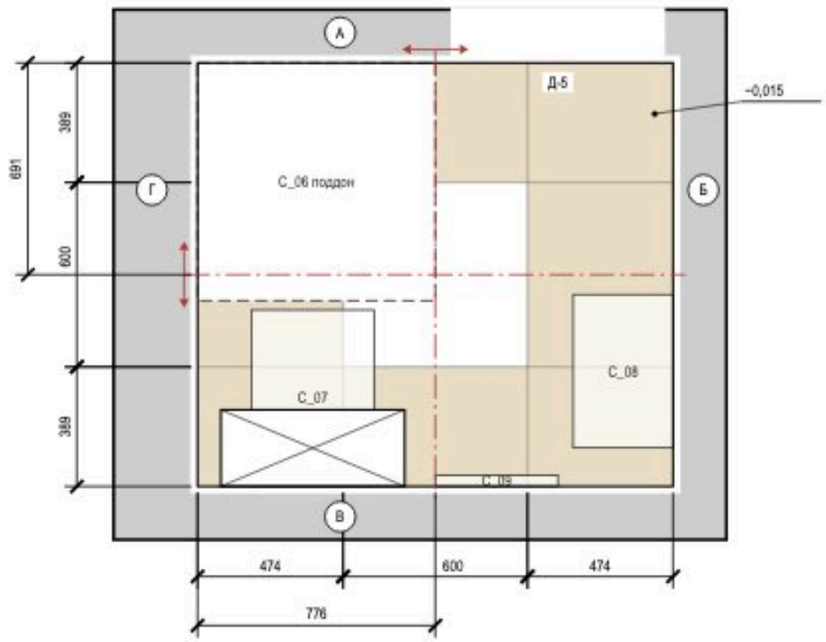

Примечания

1. Раскладка от чистовых размеров: стены санузлов теряют 10 + 5 + 9 = 24 мм на сторону (штукатурка, клей, плитка); подрезки — чистые, без шва.
2. Старт — от центра помещения (штрихпунктир, стрелки направление укладки); размер старта — от чистовых стен Г и А.
3. Раскладка пола «Прихожая» и фартука «Кухня-гостиная» на листе «Раскладка плитки. Прихожая. Фартук кухни».
4. Калибр партии не задан — до укладки замерить (рабочий размер W, ГОСТ 13996-2019) и пересчитать подрезки.
5. Количество: целые по раскладке + по одной на подрезку, запас 10 %; один артикул — одна партия и тон. Исключены поддон, короб, проёмы и места за коробом; S — по чистым граням: стены нетто = зона облицовки по ведомости отделки − место за коробом инсталляции 1,68 м² (плитку за коробом не кладут), короб — отдельной строкой.
6. Клей C2 TE S1 Ceresit CM 17; C2 TE S1 (ГОСТ Р 56387-2018), затирка CG2WA Mapei Ultracolor Plus 132; CG2WA; расход — по ТУ выбранной марки.
7. Гидроизоляция: пол и стены 200 мм от ЧП; над ванной до 2000 и 300 мм за борт, у душа — до 2000 и 500 мм за поддон (см. развёртки); акт скрытых работ, пролив 24 ч.
8. Швы пола совмещены со швами стены А; по периметру демпферная лента.
9. Отметка чистого пола −0,015, порог 15 мм; стык с соседним покрытием — по оси полотна двери.

Ведомость материалов

Материал	Класс, код	Норма расхода	Кол-во
Затирка	CG2WA Mapei Ultracolor Plus 132	(a+b)/ab·шов·t·1,6	3,1 кг
Затирка	CG2WA	(a+b)/ab·шов·t·1,6	0,7 кг
Клей	C2 TE S1 Ceresit CM 17	1,5 кг/м²·мм, слой 5	312 кг (13 меш.)
Клей	C2 TE S1	1,5 кг/м²·мм, слой 5	73 кг (3 меш.)
Гидроизоляция	обмазочная, 2 слоя: пол, стены по периметру и зоны замачивания	по ТУ	20,0 м²
Демпф. лента	по периметру пола из плитки		22,4 м

Ведомость плитки

Помещение, поверхность	Плитка, код	Формат	Шов	S, м²	Целых	Подр.	С запасом
Ванная, пол	аналог: керамогранит под травертин	600×600	2	4,43	4	12	18
Ванная, стены А–Г	аналог: керамогранит под травертин	600×1200	2	17,65	10	21	35
Ванная, короб инсталляции	аналог: керамогранит под травертин	600×1200	2	1,76	0	6	7
Санузел 2, пол	аналог: керамогранит под травертин	600×600	2	2,29	0	8	9
Санузел 2, стены А–Г	аналог: керамогранит под травертин	600×1200	2	12,38	5	19	28
Санузел 2, короб инсталляции	аналог: керамогранит под травертин	600×1200	2	1,47	1	3	5
Прихожая, пол	аналог: керамогранит ректифицированный под травертин, матовый	600×1200	2	7,13	2	10	14
Кухня-гостиная, фартук (ст. В)	аналог: керамогранит под травертин, матовый	1200×600	2	1,87	0	4	5
Итого 600×600				6,72	4	20	27
Итого 600×1200				**42,26**	**18**	**63**	**94**

Условные обозначения


- плитка целая; тонкая линия — шов
- плитка с подрезкой (размер — на цепочке)
- ось старта; стрелки — направление укладки
- сантехприбор: габарит, высота по практике
- поддон душа — плитку пола под ним не кладут
- короб инсталляции: плитка пола — до короба
- отметка чистого пола на полке выноском, м
- (А) обозначение стены А–Г (как на развёртках)

					Проект: Трёхкомнатная квартира
	Лист	№ док.	Подпись	Дата	Раскладка плитки. Планы полов
Дизайнер	Кырпан А.С.			05.10.26	


Стадия	Лист	Листов
П	30	88

выпуск 05.10.2026 № 204f23b33a · стр. 30 из 88

Фрагмент 1. Прихожая (пом. 5). Пол 600×1200, шов 2 мм, М 1:20

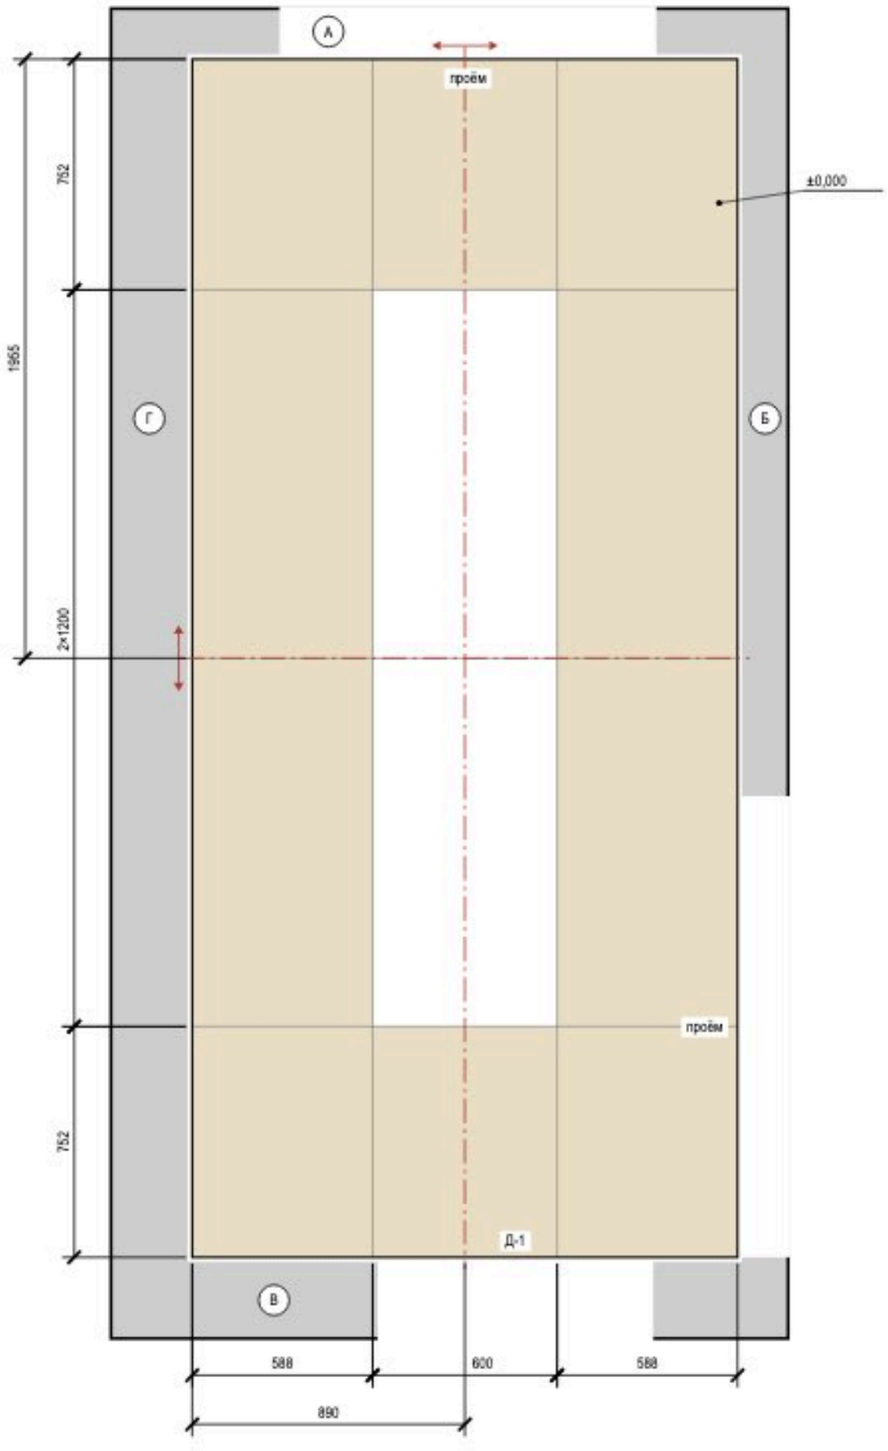

Фрагмент 2. Кухня-гостиная (пом. 6), фартук, стена В. 1200×600, шов 2 мм, М 1:20

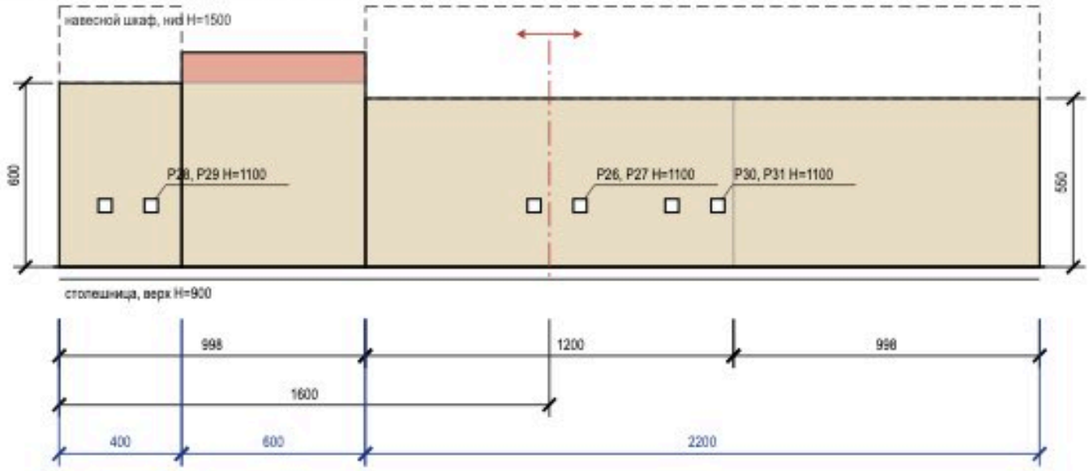

Условные обозначения

- плитка целая; тонкая линия — шов
- плитка с подрезкой (размер — на цепочке)
- ось старта; стрелки — направление укладки
- электроточка: марка и H — по листам ЭОМ
- столешница (верх)
- навесной шкаф над фартуком
- отметка чистого пола на полке выноски, м
- (А) обозначение стены А–Г (как на развёртках)

Подсчёт плитки

Поверхность	Формат	S, м²	Целых	Подр.	С запасом
Прихожая, пол	600×1200	7,13	2	10	14
Кухня-гостиная, фартук (ст. В)	1200×600	1,87	0	4	5

Сдвиг розеток фартука под раскладку

Точка (ЭОМ)	Проект: от угла / H	Под раскладку: от угла / H	Сдвиг, мм
P26, P27, P30, P31	1700, 1550, 2150, 2000 / 1100	1700, 1550, 2150, 2000 / 1175	H +75 — ось ряда
P28, P29	300, 150 / 1100	300, 150 / 1200	H +100 — ось ряда

Примечания

1. Прихожая: керамогранит 600×1200, длинная сторона — вдоль стен Б и Г, шов 2 мм, прямая раскладка от центра. Стены окрашены: раскладка от чистового контура минус штукатурка и шпаклёвка 15 мм на сторону (принято); подрезки 588 / 752 мм, срез — под плинтус.
2. Прихожая: деформационный зазор по периметру 8–10 мм под плинтусом; в проёмах — стык с соседним покрытием по оси полотна двери. Клей C2 TE S1, затирка CG2WA.
3. Фартук, Кухня-гостиная: 1200×600 горизонтально, шов 2 мм; зоны 2200 мм — 900…1450, 600 мм — 900…1600, 400 мм — 900…1500 (от столешницы до низа навесного шкафа, без шкафа — 700 мм). Старт от центра участка, подрезки 998 мм. Площадь 1,87 м² — как в ведомости отделки.
4. Фартук — после монтажа столешницы, низ на 2–3 мм выше неё, шов со столешницей — санитарный герметик; навесные шкафы — после фартука. Торцы у пенала и стены — профиль или запил 45°.
5. Фартук, Кухня-гостиная: в зоне до отм. 1600 верхний ряд подрезан 98 мм — меньше 1/3 плитки; полоса прикрыта корпусом навесного модуля и на виду не остаётся. Раскладкой не снимается: убрать подрезку можно, только выровняв низ этого модуля с соседними (1450 мм) — решение мебельщика.
6. Розетки из таблицы переносятся до черновой электрики: по высоте — на ось ряда плитки, от вертикального шва крупной плитки — не ближе 60 мм. Привязка — от левого края фартука на развёртке.
7. Клей, затирка и итог по форматам — в ведомостях листа «Раскладка плитки. Планы полов».

					Проект: Трёхкомнатная квартира
	Лист	№ док.	Подпись	Дата	
Дизайнер	Кырпан А.С.			05.10.26	Раскладка плитки. Прихожая. Фартук кухни

Стадия	Лист	Листов
П	31	88

выпуск 05.10.2026 № 204f23b33a · стр. 31 из 88



					Проект: Трёхкомнатная квартира	
	Лист	№ док.	Подпись	Дата	Визуализация. Вид сверху	Стадия / Лист / Листов
Дизайнер	Кырпан А.С.			05.10.26		П / 32 / 88

выпуск 05.10.2026 № 204f23b33a · стр. 32 из 88



					Проект: Трёхкомнатная квартира	
	Лист	№ док.	Подпись	Дата		
Дизайнер	Кырпан А.С.			05.10.26	Визуализация	Стадия / Лист / Листов
						П / 33 / 88

выпуск 05.10.2026 № 204f23b33a · стр. 33 из 88



					Проект: Трёхкомнатная квартира	
	Лист	№ док.	Подпись	Дата		
Дизайнер	Кырпан А.С.			05.10.26	Визуализация: Спальня 1	Стадия / Лист / Листов
						П / 34 / 88

выпуск 05.10.2026 № 204f23b33a · стр. 34 из 88



					Проект: Трёхкомнатная квартира
	Лист	№ док.	Подпись	Дата	
Дизайнер	Кырпан А.С.			05.10.26	Визуализация: Спальня 1

Стадия	Лист	Листов
П	35	88

выпуск 05.10.2026 № 204f23b33a · стр. 35 из 88



					Проект: Трёхкомнатная квартира
	Лист	№ док.	Подпись	Дата	
Дизайнер	Кырпан А.С.			05.10.26	Визуализация: Спальня 1

Стадия	Лист	Листов
П	36	88

выпуск 05.10.2026 № 204f23b33a · стр. 36 из 88

Развёртка стены А


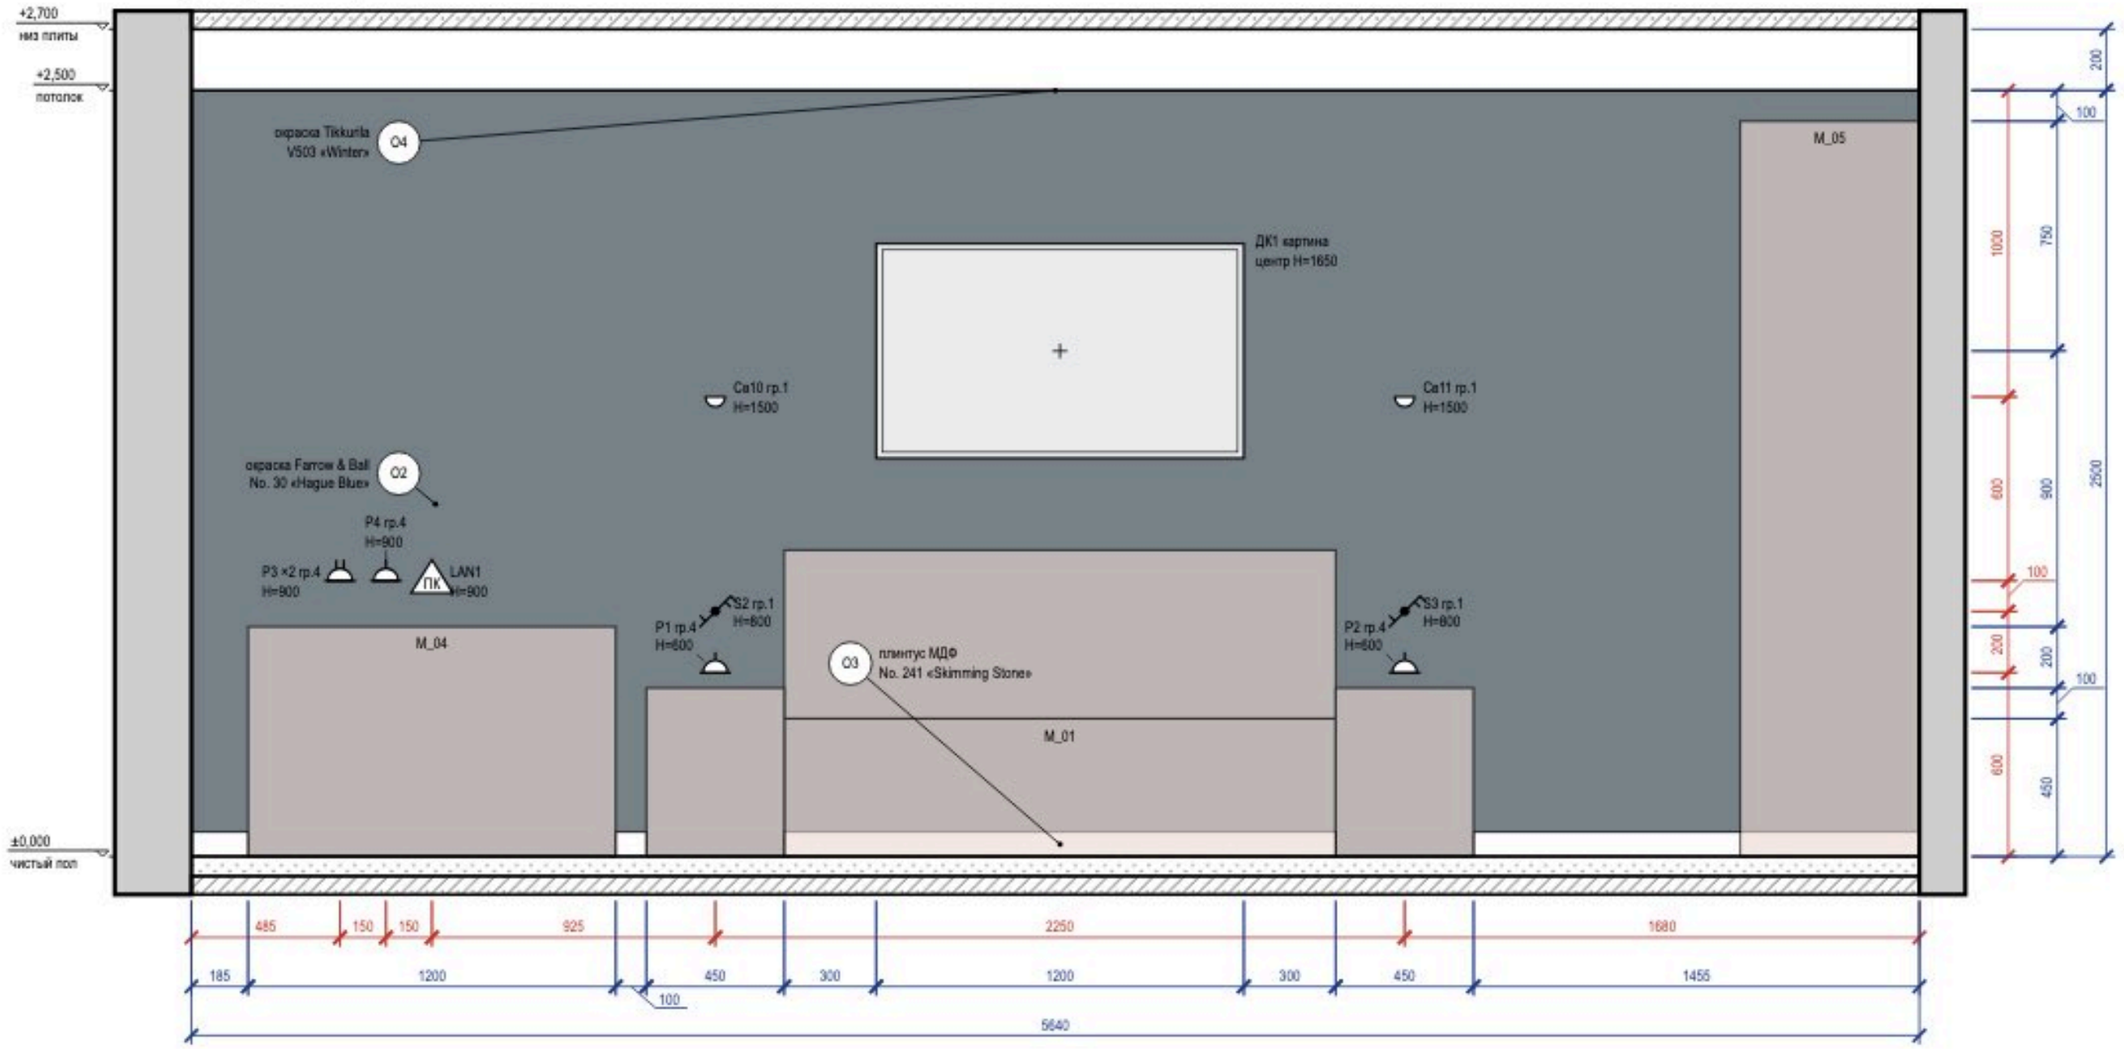


Схема развёрток (М 1:100)

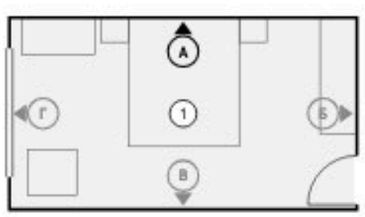

Ведомость отделки (на листе)

Марка	Поверхность	Материал, изделие	Цвет, код	Кол.
Q2	акцентная стена	окраска, Farrow & Ball Modern Emulsion, матовая, подготовка Q3	Farrow & Ball No. 30 «Hague Blue»	14,1 м²
Q3	плинтус	плинтус МДФ, h 80 мм, аналог: плинтус МДФ под покраску 80×16	Farrow & Ball No. 241 «Skimming Stone»	3,5 м
Q4	потолок	окраска, Tikkurila Anti-Reflex 2, глубокоматовая, подготовка Q3	Tikkurila V503 «Winter»	17,8 м²

Визуализация этой стены — лист 35



Примечания

1. Размеры — в мм от чистовых поверхностей стен; условные обозначения и общие указания — лист 2.
2. Картины и зеркала крепить к основанию по паспорту изделия (закладные и анкеры — в перечне скрытых работ); крест — ось центра предмета.
3. Потолок на развёртках — по нижнему уровню У1; другие уровни потолка помещения: У2 +2,600.

					Проект: Трёхкомнатная квартира
	Лист	№ док.	Подпись	Дата	Развёртка стены А. Спальня 1 (пом. 1)
Дизайнер	Кырпан А.С.			05.10.26	

Стадия	Лист	Листов
П	37	88

выпуск 05.10.2026 № 204f23b33a · стр. 37 из 88

Развёртка стены Б


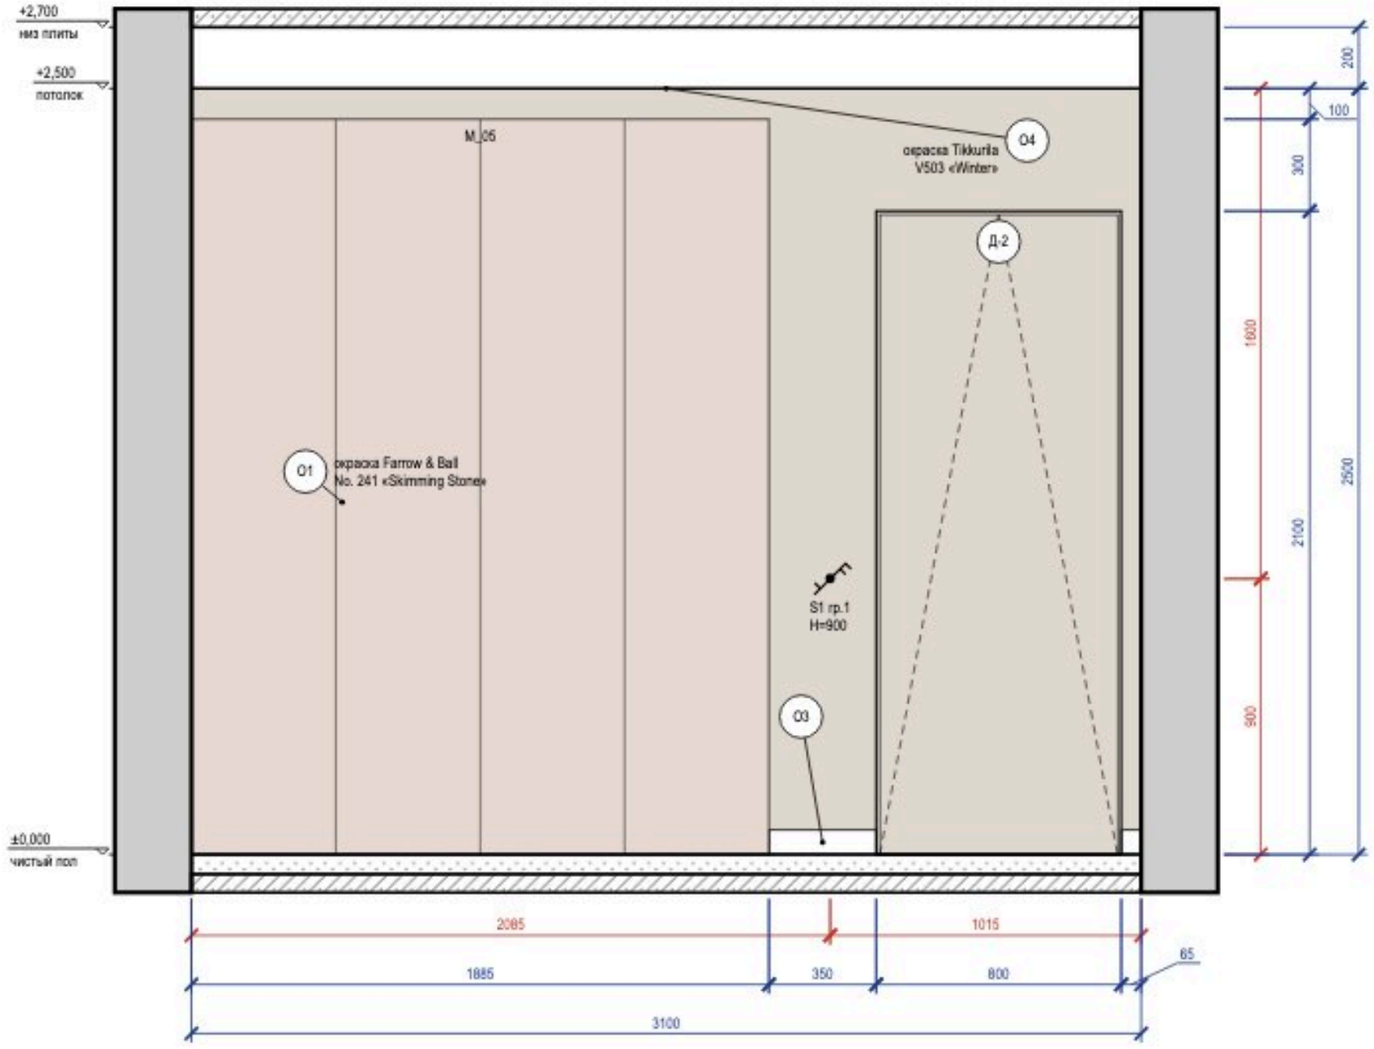



Схема развёрток (М 1:100)

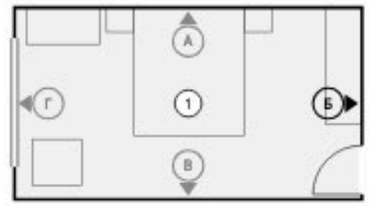

Ведомость отделки (на листе)

Марка	Поверхность	Материал, изделие	Цвет, код	Кол.
О1	стены	окраска, Farrow & Ball Modern Emulsion, матовая, подготовка Q3	Farrow & Ball No. 241 «Skimming Stone»	6,1 м²
О3	плинтус	плинтус МДФ, h 80 мм, аналог: плинтус МДФ под покраску 80×16	Farrow & Ball No. 241 «Skimming Stone»	0,4 м
О4	потолок	окраска, Tikkurila Anti-Reflex 2, глубокоматовая, подготовка Q3	Tikkurila V503 «Winter»	17,8 м²

Визуализация этой стены — лист 36

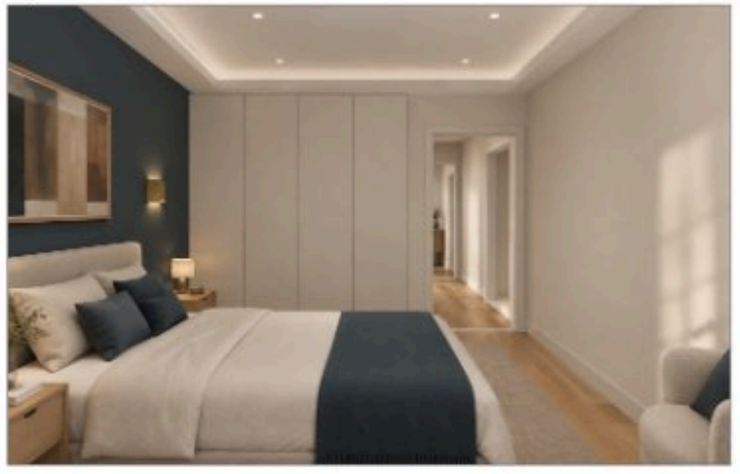

Примечания

1. Размеры — в мм от чистовых поверхностей стен; условные обозначения и общие указания — лист 2.
2. Двери скрытого монтажа — полотно в плоскости стены, отделка стены по полотну, плинтус прерывается у короба (узел — на листе узлов).
3. Потолок на развёртках — по нижнему уровню У1; другие уровни потолка помещения: У2 +2,600.

					Проект: Трёхкомнатная квартира
	Лист	№ док.	Подпись	Дата	
Дизайнер	Кырпан А.С.			05.10.26	Развёртка стены Б. Спальня 1 (пом. 1)

Стадия	Лист	Листов
П	38	88

выпуск 05.10.2026 № 204f23b33a · стр. 38 из 88

Развёртка стены В


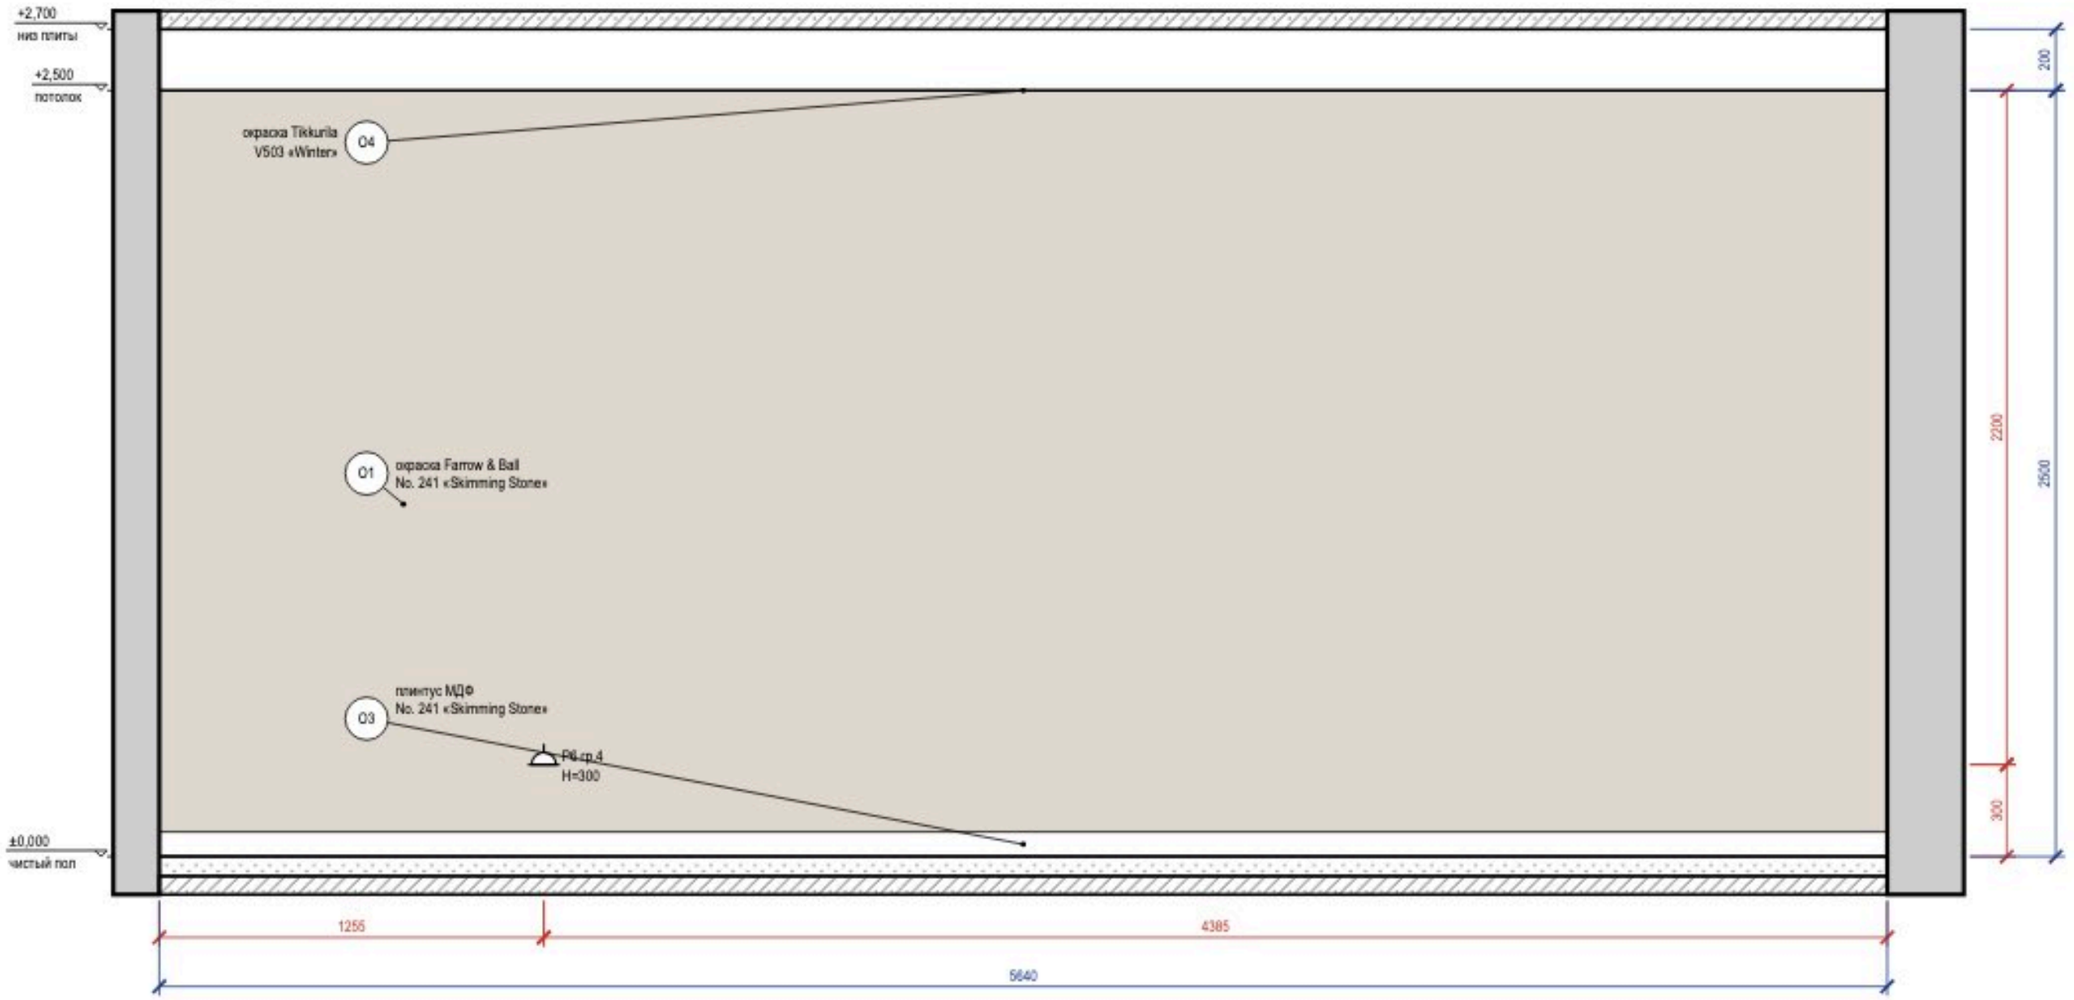


Схема развёрток (М 1:100)

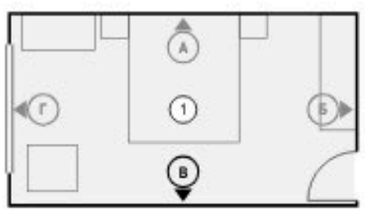

Ведомость отделки (на листе)

Марка	Поверхность	Материал, изделие	Цвет, код	Кол.
О1	стены	окраска, Farrow & Ball Modern Emulsion, матовая, подготовка Q3	Farrow & Ball No. 241 «Skimming Stone»	14,1 м²
О3	плинтус	плинтус МДФ, h 80 мм, аналог: плинтус МДФ под покраску 80×16	Farrow & Ball No. 241 «Skimming Stone»	5,6 м
О4	потолок	окраска, Tikkurila Anti-Reflex 2, глубокоматовая, подготовка Q3	Tikkurila V503 «Winter»	17,8 м²

Примечания

1. Размеры — в мм от чистовых поверхностей стен; условные обозначения и общие указания — лист 2.
2. Потолок на развёртках — по нижнему уровню У1; другие уровни потолка помещения: У2 +2,600.

					Проект: Трёхкомнатная квартира
	Лист	№ док.	Подпись	Дата	
Дизайнер	Кырпан А.С.			05.10.26	Развёртка стены В. Спальня 1 (пом. 1)

Стадия	Лист	Листов
П	39	88

выпуск 05.10.2026 № 204f23b33a · стр. 39 из 88

Развёртка стены Г


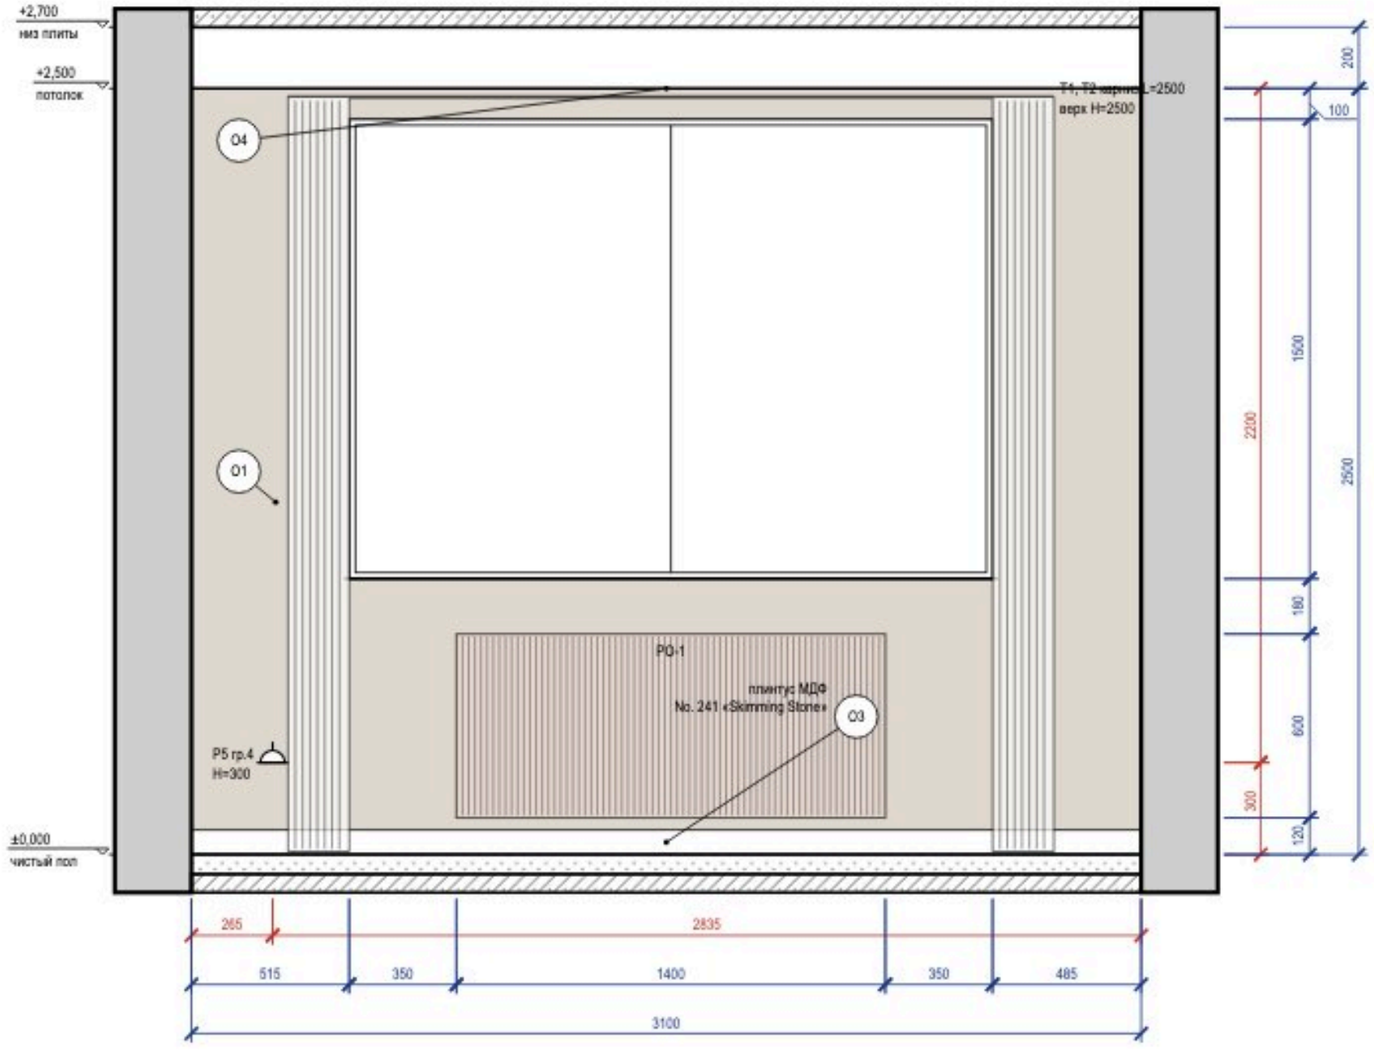



Схема развёрток (М 1:100)

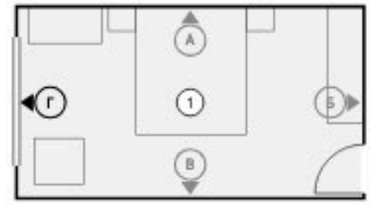

Ведомость отделки (на листе)

Марка	Поверхность	Материал, изделие	Цвет, код	Кол.
О1	стены	окраска, Farrow & Ball Modern Emulsion, матовая, подготовка Q3	Farrow & Ball No. 241 «Skimming Stone»	4,6 м²
О3	плинтус	плинтус МДФ, h 80 мм, аналог: плинтус МДФ под покраску 80×16	Farrow & Ball No. 241 «Skimming Stone»	3,1 м
О4	потолок	окраска, Tikkurila Anti-Reflex 2, глубокоматовая, подготовка Q3	Tikkurila V503 «Winter»	17,8 м²

Визуализация этой стены — лист 34

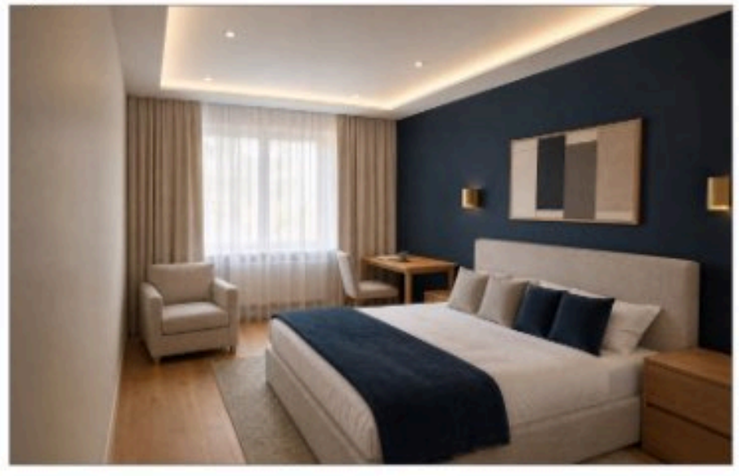

Примечания

1. Размеры — в мм от чистовых поверхностей стен; условные обозначения и общие указания — лист 2.
2. Карнизы (шины) — по ведомости текстиля декоратора; длина L и верх H — по развёртке, крепление — до окраски потолка.
3. Потолок на развёртках — по нижнему уровню У1; другие уровни потолка помещения: У2 +2,600.

					Проект: Трёхкомнатная квартира
	Лист	№ док.	Подпись	Дата	Развёртка стены Г. Спальня 1 (пом. 1)
Дизайнер	Кырпан А.С.			05.10.26	

Стадия	Лист	Листов
П	40	88

выпуск 05.10.2026 № 204f23b33a · стр. 40 из 88



					Проект: Трёхкомнатная квартира	
	Лист	№ док.	Подпись	Дата	Визуализация ванной	Стадия / Лист / Листов
Дизайнер	Кырпан А.С.			05.10.26		П / 41 / 88

выпуск 05.10.2026 № 204f23b33a · стр. 41 из 88



					Проект: Трёхкомнатная квартира	
	Лист	№ док.	Подпись	Дата		
Дизайнер	Кырпан А.С.			05.10.26	Визуализация ванной	Стадия: П; Лист: 42; Листов: 88

выпуск 05.10.2026 № 204f23b33a · стр. 42 из 88



					Проект: Трёхкомнатная квартира	
	Лист	№ док.	Подпись	Дата		
Дизайнер	Кырпан А.С.			05.10.26	Визуализация ванной	Стадия: П; Лист: 43; Листов: 88


выпуск 05.10.2026 № 204f23b33a · стр. 43 из 88



					Проект: Трёхкомнатная квартира	
	Лист	№ док.	Подпись	Дата	Визуализация ванной	Стадия / Лист / Листов
Дизайнер	Кырпан А.С.			05.10.26		П / 44 / 88

выпуск 05.10.2026 № 204f23b33a · стр. 44 из 88

Развёртка стены А

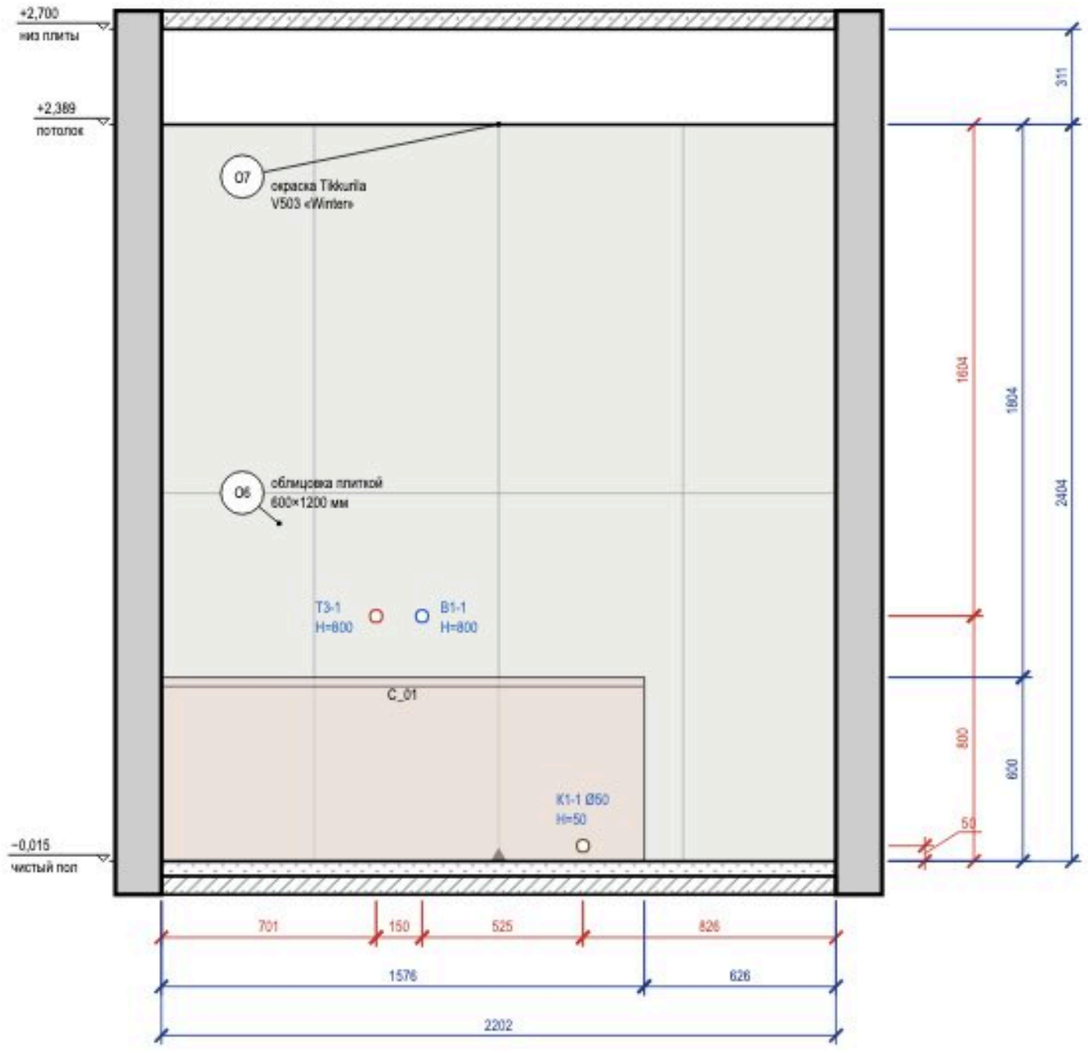

Развёртка стены Б

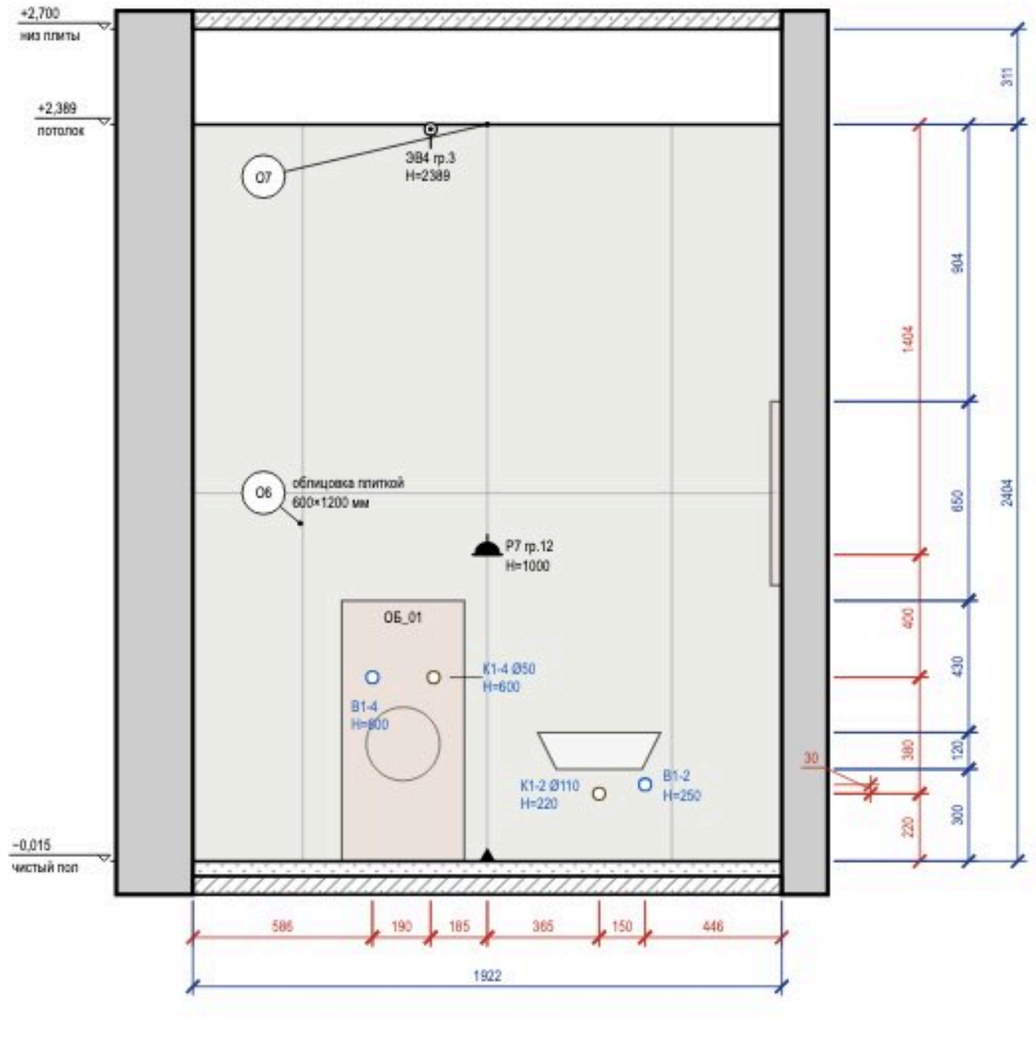



Схема развёрток (М 1:100)



Ведомость отделки (на листе)

Марка	Поверхность	Материал, изделие	Цвет, код	Кол.
О6	стены	облицовка плиткой, 600×1200×9 мм, аналог: керамогранит под травертин, матовый, затирка CG2WA		9,9 м²
О7	потолок	окраска, Tikkurila Luja 7, матовая, подготовка Q3	Tikkurila V503 «Winter»	4,4 м²

Визуализация этой стены — лист 41

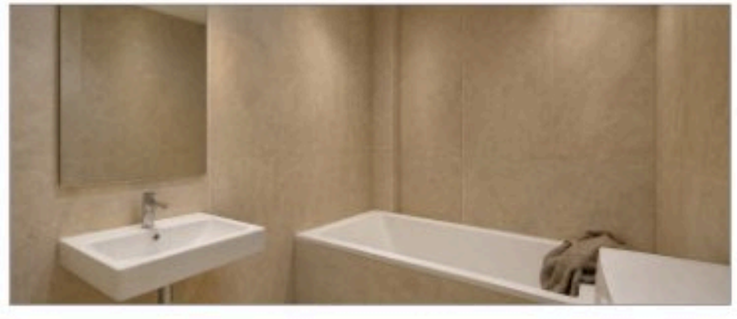

Примечания

1. Размеры — в мм от чистовых поверхностей стен; условные обозначения и общие указания — лист 2.
2. Схема мебели, приборов и декора не является технической документацией для производства мебели; габариты — по паспортам изделий.
3. Выводы ВК — коды и высоты по листу выводов сантехники.
4. Облицовка — по сетке швов 2 мм, раскладка от оси стены (треугольник у пола), целые ряды от пола; подрезки — по листу раскладки плитки.
5. Гидроизоляция в 2 слоя, заход на стены 200 мм — до облицовки, с актом скрытых работ и тестом проливом (узел — на листе узлов).

					Проект: Трёхкомнатная квартира
	Лист	№ док.	Подпись	Дата	Развёртки стен А, Б. Ванная (пом. 2)
Дизайнер	Кырпан А.С.			05.10.26	

Стадия	Лист	Листов
П	45	88

выпуск 05.10.2026 № 204f23b33a · стр. 45 из 88

Развёртка стены В

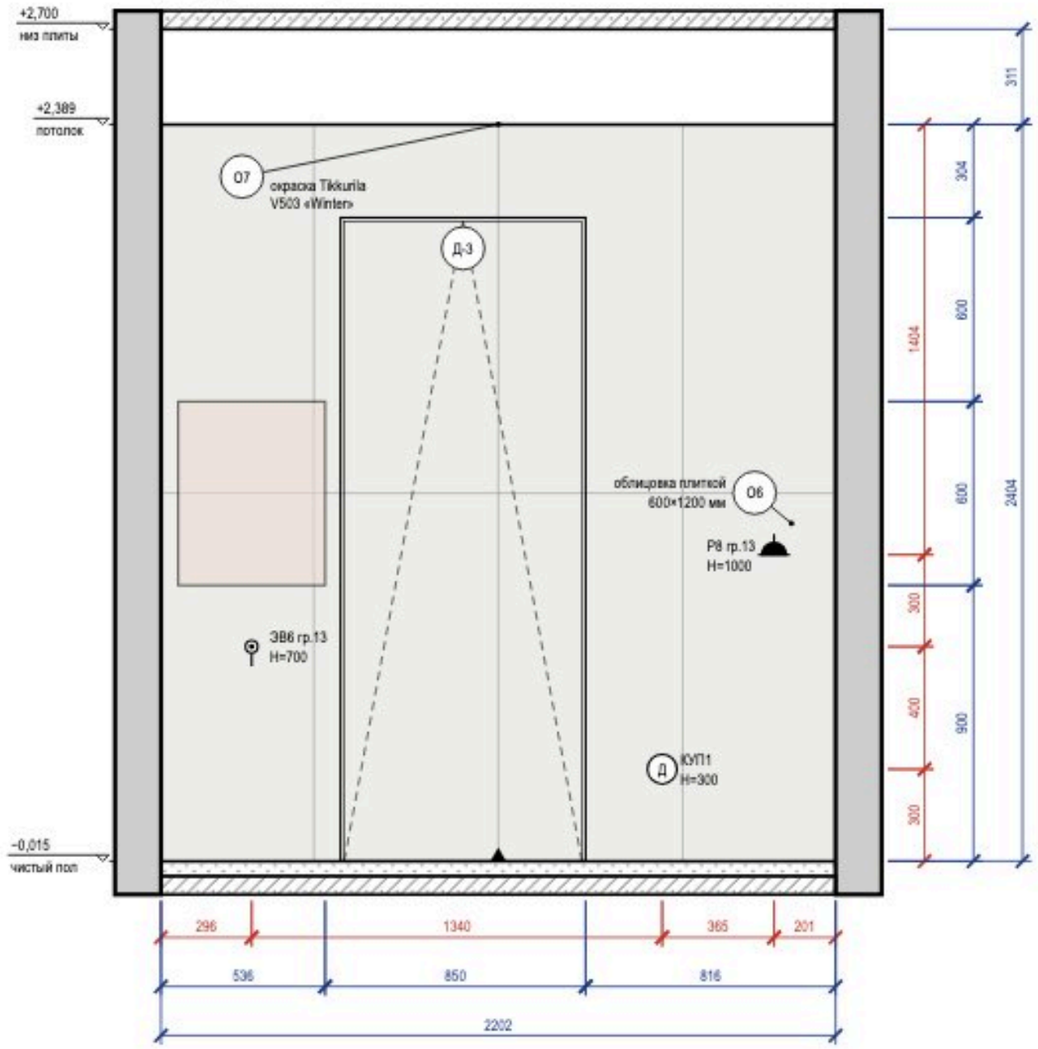


Схема развёрток (М 1:100)



Ведомость отделки (на листе)

Марка	Поверхность	Материал, изделие	Цвет, код	Кол.
О6	стены	облицовка плиткой, 600×1200×9 мм, аналог: керамогранит под травертин, матовый, затирка CG2WA		3,6 м²
О7	потолок	окраска, Tikkurila Luja 7, матовая, подготовка Q3	Tikkurila V503 «Winter»	4,4 м²

Визуализация этой стены — лист 43



Примечания

1. Размеры — в мм от чистовых поверхностей стен; условные обозначения и общие указания — лист 2.
2. Схема мебели, приборов и декора не является технической документацией для производства мебели; габариты — по паспортам изделий.
3. Облицовка — по сетке швов 2 мм, раскладка от оси стены (треугольник у пола), целые ряды от пола; подрезки — по листу раскладки плитки.
4. Гидроизоляция в 2 слоя, заход на стены 200 мм — до облицовки, с актом скрытых работ и тестом проливом (узел — на листе узлов).
5. Двери скрытого монтажа — полотно в плоскости стены, отделка стены по полотну, плинтус прерывается у короба (узел — на листе узлов).

					Проект: Трёхкомнатная квартира			
	Лист	№ док.	Подпись	Дата	Развёртка стены В. Ванная (пом. 2)	Стадия	Лист	Листов
Дизайнер	Кырпан А.С.			05.10.26		П	46	88

выпуск 05.10.2026 № 204f23b33a · стр. 46 из 88

Развёртка стены Г

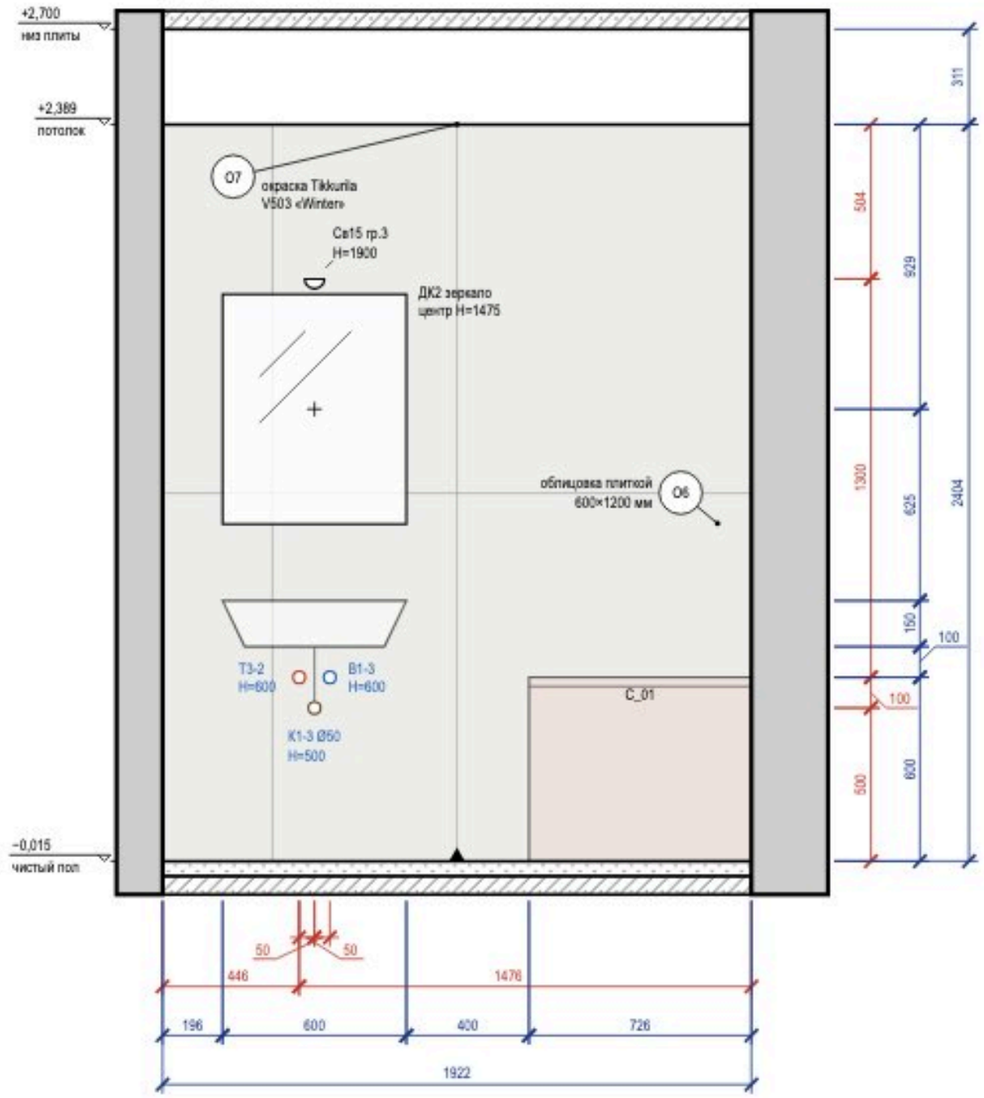



Схема развёрток (М 1:100)



Ведомость отделки (на листе)

Марка	Поверхность	Материал, изделие	Цвет, код	Кол.
О6	стены	облицовка плиткой, 600×1200×9 мм, аналог: керамогранит под травертин, матовый, затирка CG2WA		4,6 м²
О7	потолок	окраска, Tikkurila Luja 7, матовая, подготовка Q3	Tikkurila V503 «Winter»	4,4 м²

Визуализация этой стены — лист 44

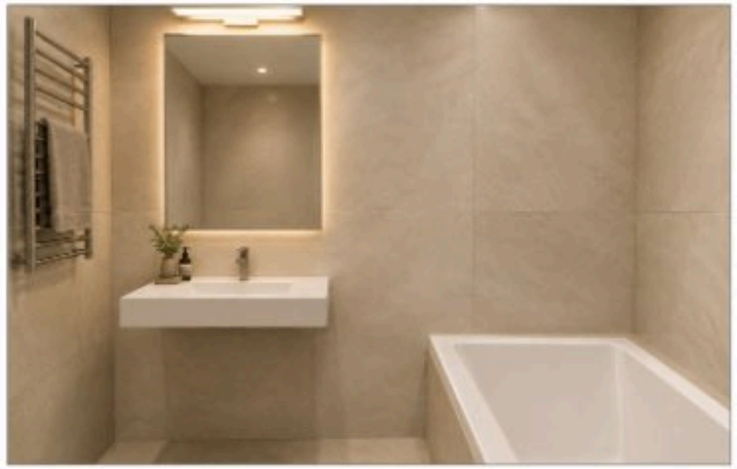


Примечания

1. Размеры — в мм от чистовых поверхностей стен; условные обозначения и общие указания — лист 2.
2. Схема мебели, приборов и декора не является технической документацией для производства мебели; габариты — по паспортам изделий.
3. Выводы ВК — коды и высоты по листу выводов сантехники.
4. Облицовка — по сетке швов 2 мм, раскладка от оси стены (треугольник у пола), целые ряды от пола; подрезки — по листу раскладки плитки.
5. Гидроизоляция в 2 слоя, заход на стены 200 мм — до облицовки, с актом скрытых работ и тестом проливом (узел — на листе узлов).
6. Картины и зеркала крепить к основанию по паспорту изделия (закладные и анкеры — в перечне скрытых работ); крест — ось центра предмета.


					Проект: Трёхкомнатная квартира			
	Лист	№ док.	Подпись	Дата	Развёртка стены Г. Ванная (пом. 2)	Стадия	Лист	Листов
Дизайнер	Кырпан А.С.			05.10.26		П	47	88

выпуск 05.10.2026 № 204f23b33a · стр. 47 из 88

Развёртка стены А

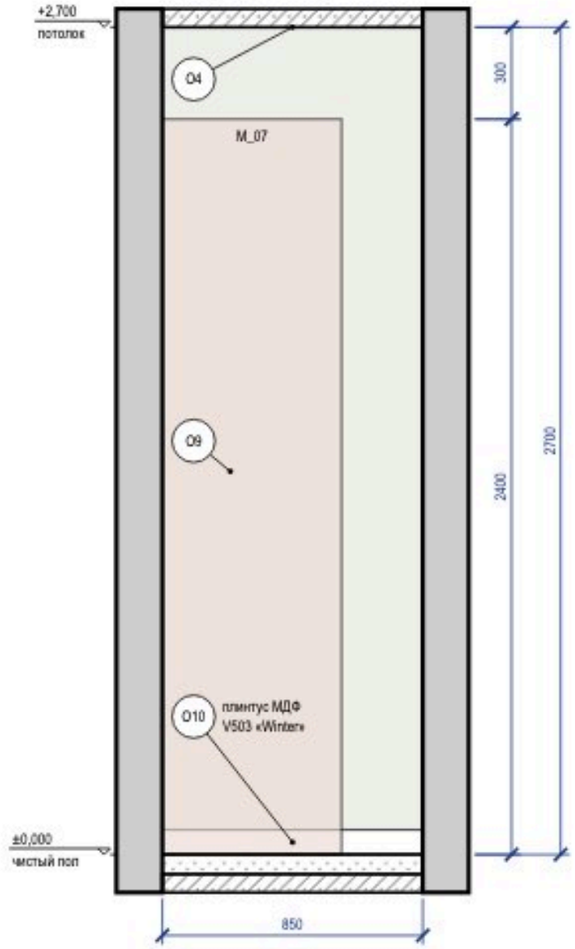

Развёртка стены В

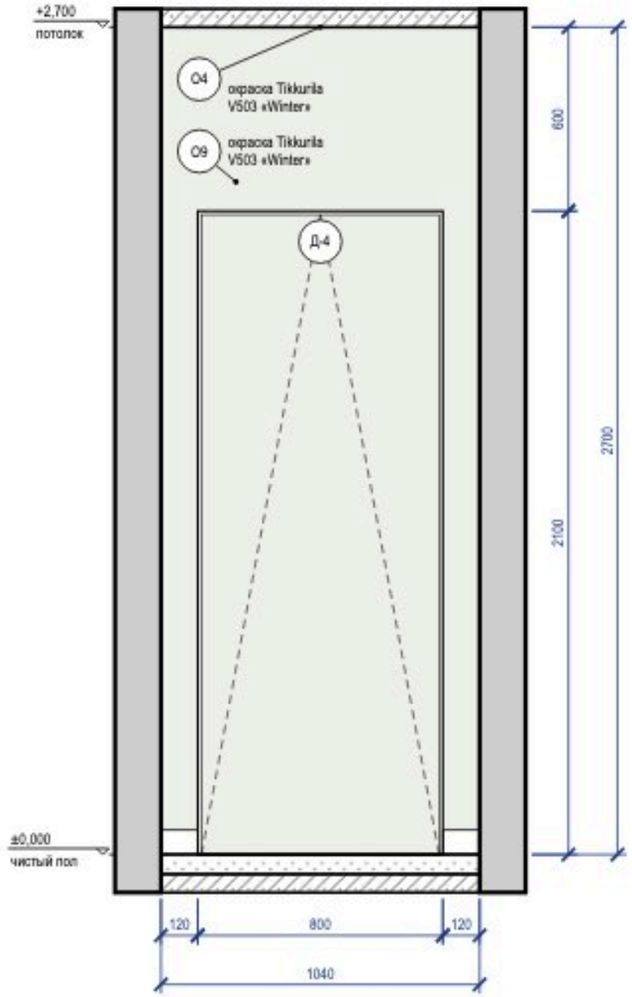

Развёртка стены Г

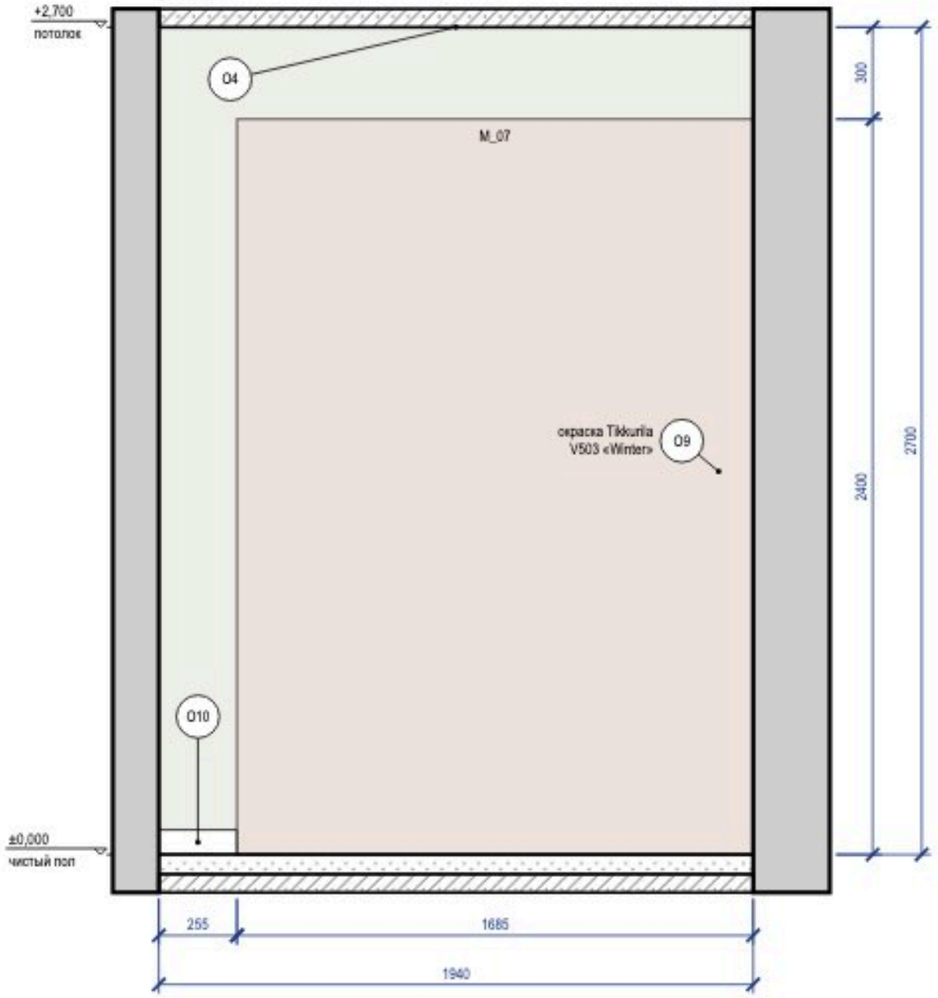


Схема развёрток (М 1:100)



Ведомость отделки (на листе)

Марка	Поверхность	Материал, изделие	Цвет, код	Кол.
О4	потолок	окраска, Tikkurila Anti-Reflex 2, глубокоматовая, подготовка Q3	Tikkurila V503 «Winter»	1,9 м²
О9	стены	окраска, Tikkurila Harmony, матовая, подготовка Q3	Tikkurila V503 «Winter»	8,7 м²
О10	плинтус	плинтус МДФ, h 80 мм, аналог: плинтус МДФ под покраску 80×16	Tikkurila V503 «Winter»	1,3 м

Примечания

1. Размеры — в мм от чистовых поверхностей стен; условные обозначения и общие указания — лист 2.
2. Двери скрытого монтажа — полотно в плоскости стены, отделка стены по полотну, плинтус прерывается у короба (узел — на листе узлов).

					Проект: Трёхкомнатная квартира	
	Лист	№ док.	Подпись	Дата		
Дизайнер	Кырпан А.С.			05.10.26	Развёртки стен. Гардеробная (пом. 3)	Стадия: П; Лист: 48; Листов: 88

выпуск 05.10.2026 № 204f23b33a · стр. 48 из 88



					Проект: Трёхкомнатная квартира	
	Лист	№ док.	Подпись	Дата		
Дизайнер	Кырпан А.С.			05.10.26	Визуализация: Спальня 2	Стадия / Лист / Листов
						П / 49 / 88

выпуск 05.10.2026 № 204f23b33a · стр. 49 из 88



					Проект: Трёхкомнатная квартира
	Лист	№ док.	Подпись	Дата	
Дизайнер	Кырпан А.С.			05.10.26	Визуализация: Спальня 2

Стадия	Лист	Листов
П	50	88

выпуск 05.10.2026 № 204f23b33a · стр. 50 из 88




					Проект: Трёхкомнатная квартира
	Лист	№ док.	Подпись	Дата	
Дизайнер	Кырпан А.С.			05.10.26	Визуализация: Спальня 2

Стадия	Лист	Листов
П	51	88

выпуск 05.10.2026 № 204f23b33a · стр. 51 из 88

Развёртка стены А

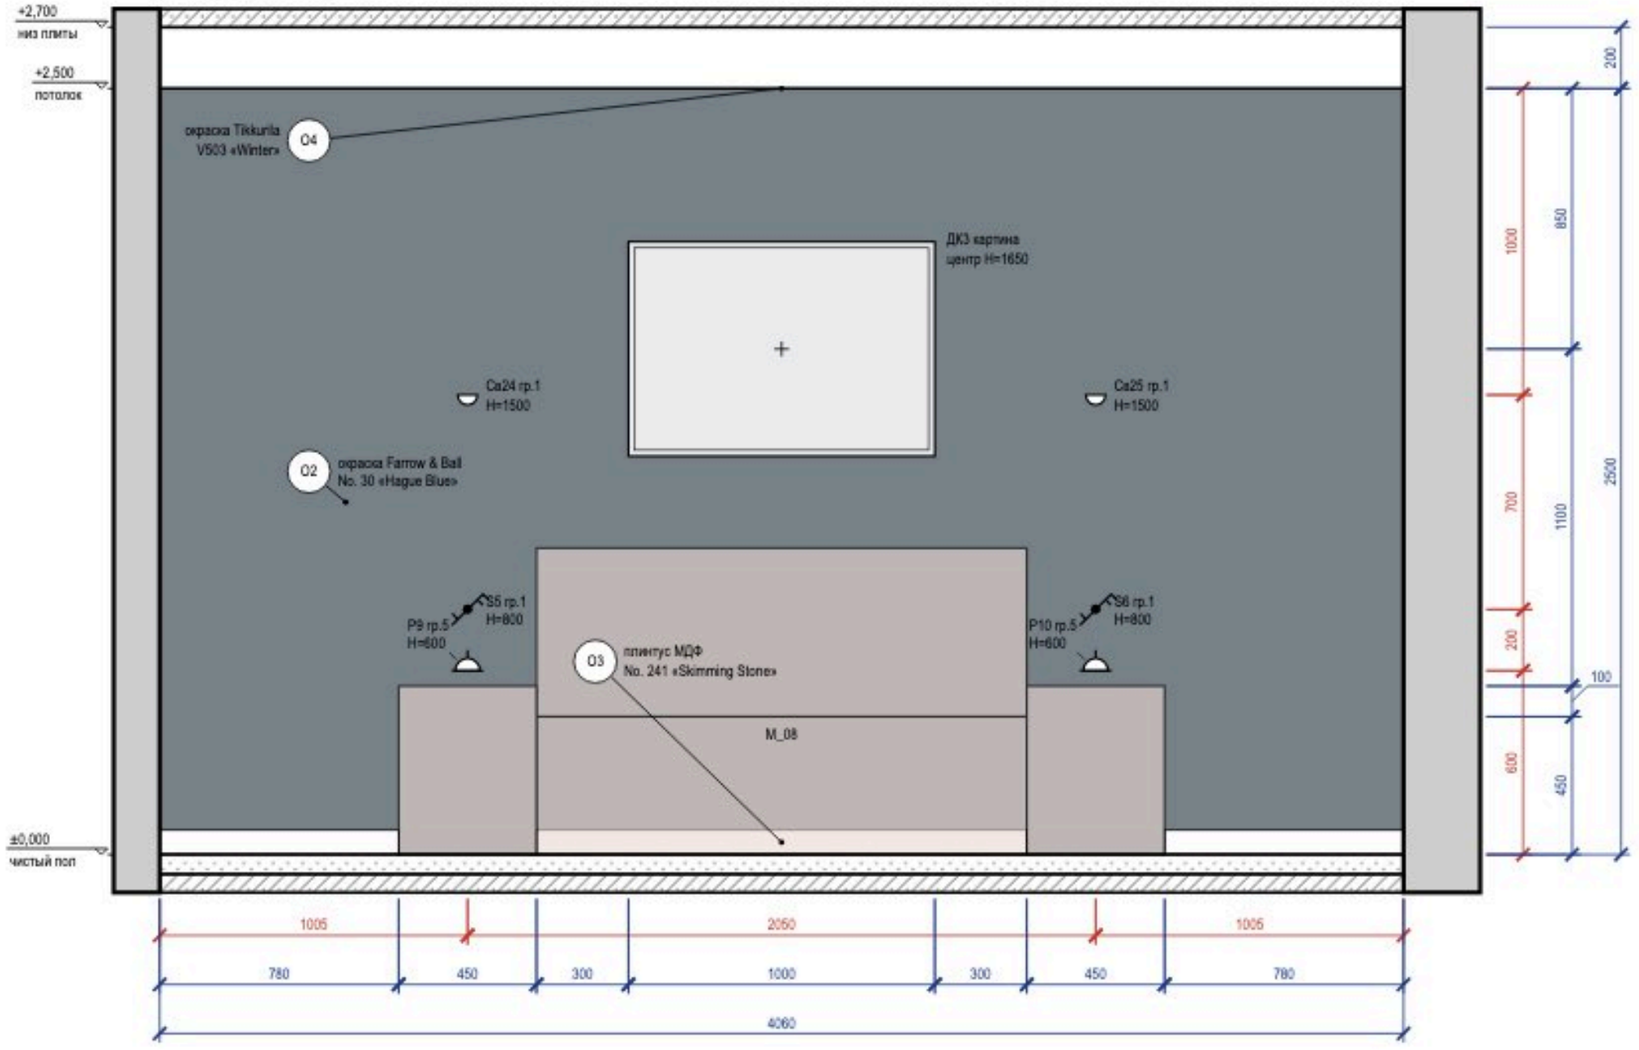

Визуализация этой стены — лист 50

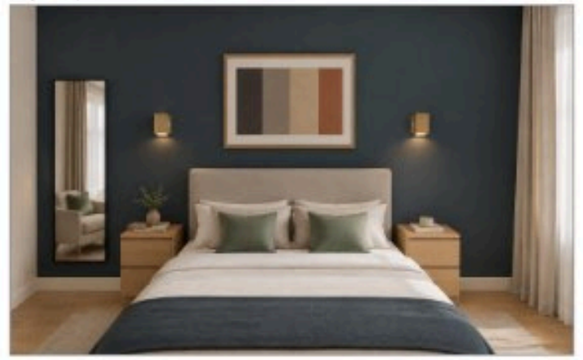


Схема развёрток (М 1:100)



Ведомость отделки (на листе)

Марка	Поверхность	Материал, изделие	Цвет, код	Кол.
О2	акцентная стена	окраска, Farrow & Ball Modern Emulsion, матовая, подготовка Q3	Farrow & Ball No. 30 «Hague Blue»	10,2 м²
О3	плинтус	плинтус МДФ, h 80 мм, аналог: плинтус МДФ под покраску 80×16	Farrow & Ball No. 241 «Skimming Stone»	3,2 м
О4	потолок	окраска, Tikkurila Anti-Reflex 2, глубокоматовая, подготовка Q3	Tikkurila V503 «Winter»	12,8 м²

Примечания

1. Размеры — в мм от чистовых поверхностей стен; условные обозначения и общие указания — лист 2.
2. Картины и зеркала крепить к основанию по паспорту изделия (закладные и анкеры — в перечне скрытых работ); «крест — ось центра предмета.
3. Потолок на развёртках — по нижнему уровню У1; другие уровни потолка помещения: У2 +2,600.

					Проект: Трёхкомнатная квартира			
	Лист	№ док.	Подпись	Дата	Развёртка стены А. Спальня 2 (пом. 4)	Стадия	Лист	Листов
Дизайнер	Кырпан А.С.			05.10.26		П	52	88

выпуск 05.10.2026 № 204f23b33a · стр. 52 из 88

Развёртка стены Б

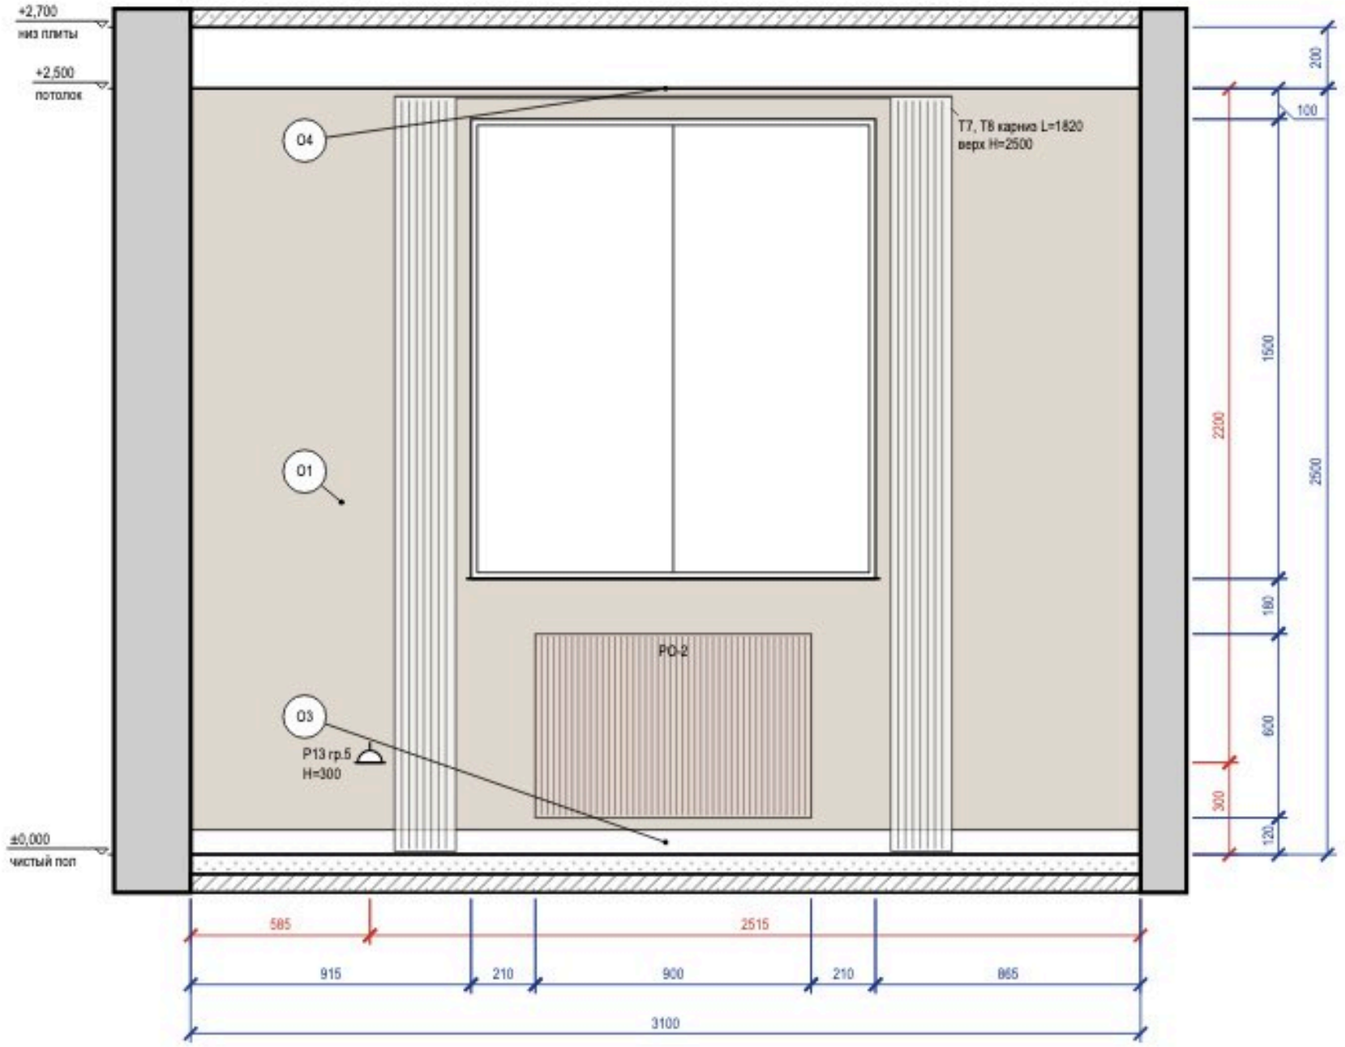


Схема развёрток (М 1:100)



Ведомость отделки (на листе)

Марка	Поверхность	Материал, изделие	Цвет, код	Кол.
О1	стены	окраска, Farrow & Ball Modern Emulsion, матовая, подготовка Q3	Farrow & Ball No. 241 «Skimming Stone»	5,8 м²
О3	плинтус	плинтус МДФ, h 80 мм, аналог: плинтус МДФ под покраску 80×16	Farrow & Ball No. 241 «Skimming Stone»	3,1 м
О4	потолок	окраска, Tikkurila Anti-Reflex 2, глубокоматовая, подготовка Q3	Tikkurila V503 «Winter»	12,8 м²

Визуализация этой стены — лист 49



Примечания

1. Размеры — в мм от чистовых поверхностей стен; условные обозначения и общие указания — лист 2.
2. Карнизы (шины) — по ведомости текстиля декоратора; длина L и верх Н — по развёртке, крепление — до окраски потолка.
3. Потолок на развёртках — по нижнему уровню У1; другие уровни потолка помещения: У2 +2,600.

					Проект: Трёхкомнатная квартира
	Лист	№ док.	Подпись	Дата	
Дизайнер	Кырпан А.С.			05.10.26	Развёртка стены Б. Спальня 2 (пом. 4)

Стадия	Лист	Листов
П	53	88

выпуск 05.10.2026 № 204f23b33a · стр. 53 из 88

Развёртка стены В

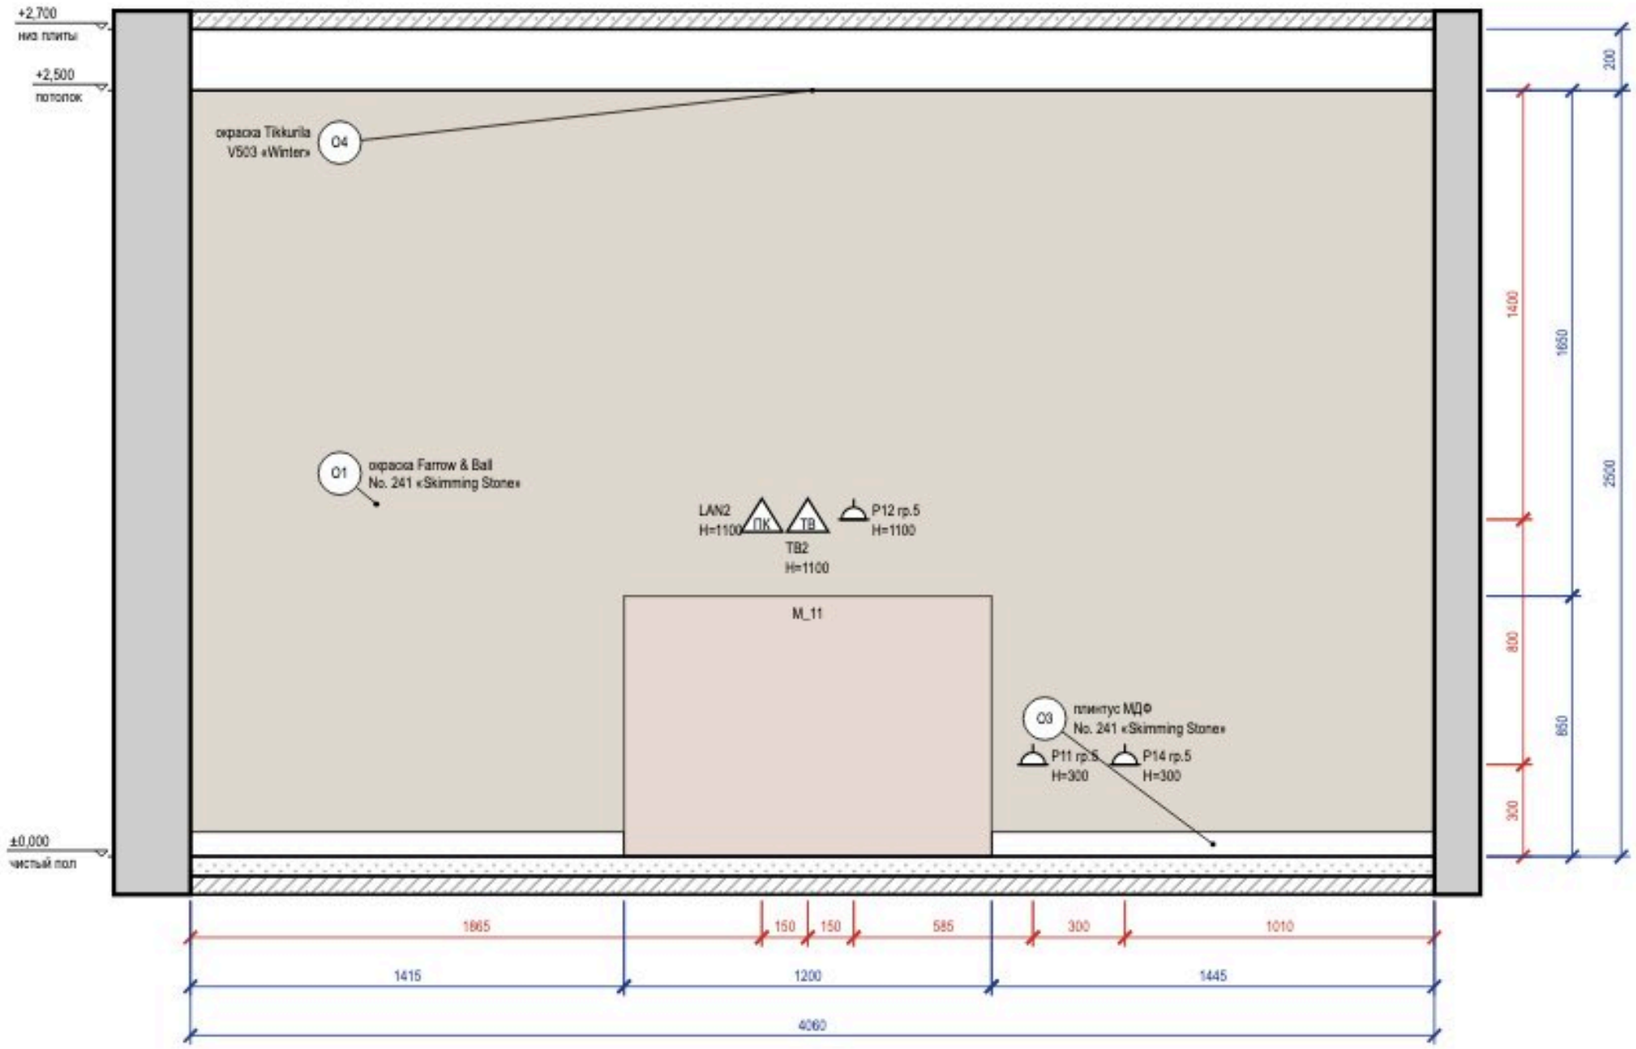


Схема развёрток (М 1:100)



Ведомость отделки (на листе)

Марка	Поверхность	Материал, изделие	Цвет, код	Кол.
O1	стены	окраска, Farrow & Ball Modern Emulsion, матовая, подготовка Q3	Farrow & Ball No. 241 «Skimming Stone»	10,2 м²
O3	плинтус	плинтус МДФ, h 80 мм, аналог: плинтус МДФ под покраску 80×16	Farrow & Ball No. 241 «Skimming Stone»	2,9 м
O4	потолок	окраска, Tikkurila Anti-Reflex 2, глубокоматовая, подготовка Q3	Tikkurila V503 «Winter»	12,8 м²

Примечания

1. Размеры — в мм от чистовых поверхностей стен; условные обозначения и общие указания — лист 2.
2. Потолок на развёртках — по нижнему уровню У1; другие уровни потолка помещения: У2 +2,600.

					Проект: Трёхкомнатная квартира
	Лист	№ док.	Подпись	Дата	Развёртка стены В. Спальня 2 (пом. 4)
Дизайнер	Кырпан А.С.			05.10.26	

Стадия	Лист	Листов
П	54	88

выпуск 05.10.2026 № 204f23b33a · стр. 54 из 88

Развёртка стены Г

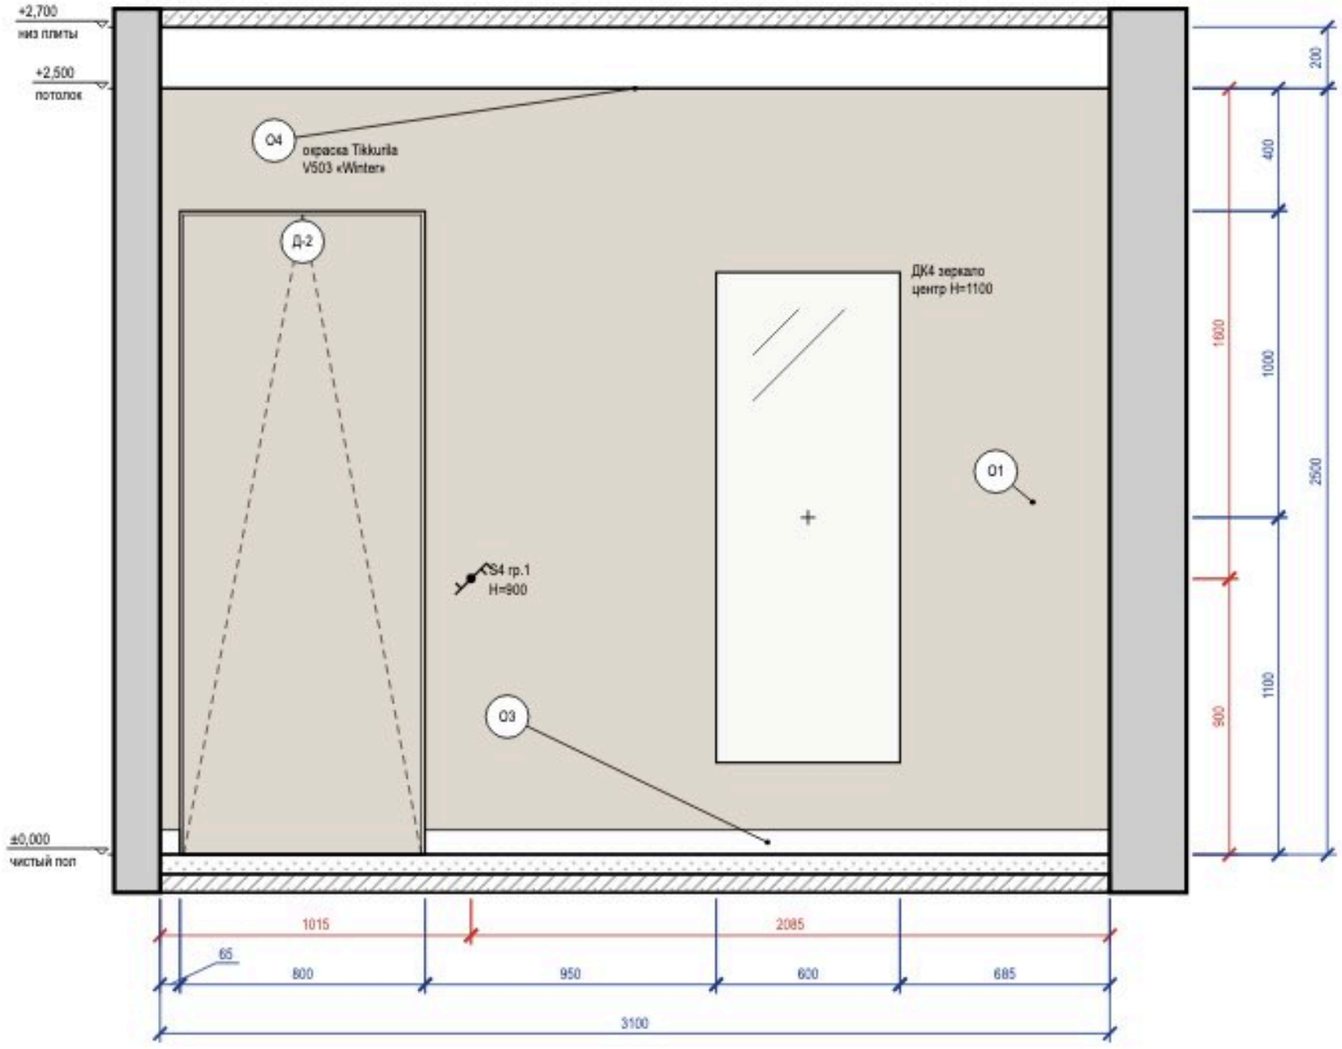



Схема развёрток (М 1:100)



Ведомость отделки (на листе)

Марка	Поверхность	Материал, изделие	Цвет, код	Кол.
О1	стены	окраска, Farrow & Ball Modern Emulsion, матовая, подготовка Q3	Farrow & Ball No. 241 «Skimming Stone»	6,1 м²
О3	плинтус	плинтус МДФ, h 80 мм, аналог: плинтус МДФ под покраску 80×16	Farrow & Ball No. 241 «Skimming Stone»	2,3 м
О4	потолок	окраска, Tikkurila Anti-Reflex 2, глубокоматовая, подготовка Q3	Tikkurila V503 «Winter»	12,8 м²

Визуализация этой стены — лист 51

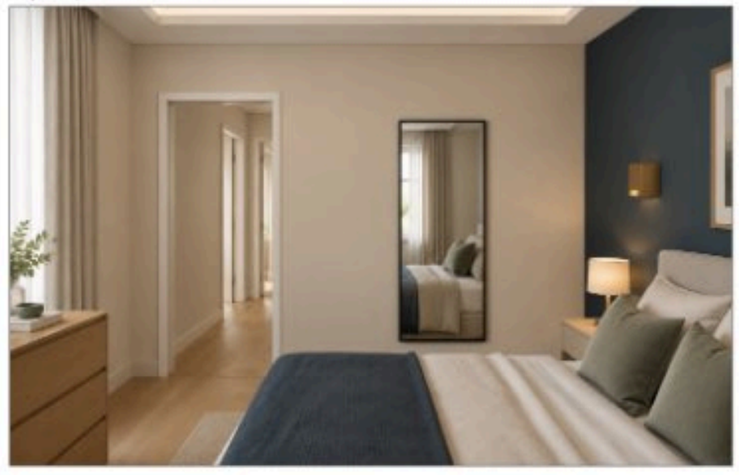

Примечания

1. Размеры — в мм от чистовых поверхностей стен; условные обозначения и общие указания — лист 2.
2. Картины и зеркала крепить к основанию по паспорту изделия (закладные и анкеры — в перечне скрытых работ); крест — ось центра предмета.
3. Двери скрытого монтажа — полотно в плоскости стены, отделка стены по полотну, плинтус прерывается у короба (узел — на листе узлов).
4. Потолок на развёртках — по нижнему уровню У1; другие уровни потолка помещения: У2 +2,600.

					Проект: Трёхкомнатная квартира
	Лист	№ док.	Подпись	Дата	Развёртка стены Г. Спальня 2 (пом. 4)
Дизайнер	Кырпан А.С.			05.10.26	

Стадия	Лист	Листов
П	55	88



					Проект: Трёхкомнатная квартира
	Лист	№ док.	Подпись	Дата	
Дизайнер	Кырпан А.С.			05.10.26	Визуализация прихожей

Стадия	Лист	Листов
П	56	88

выпуск 05.10.2026 № 204f23b33a · стр. 56 из 88



					Проект: Трёхкомнатная квартира	
	Лист	№ док.	Подпись	Дата		
Дизайнер	Кырпан А.С.			05.10.26	Визуализация прихожей	Стадия / Лист / Листов
						П / 57 / 88

выпуск 05.10.2026 № 204f23b33a · стр. 57 из 88

Развёртка стены А


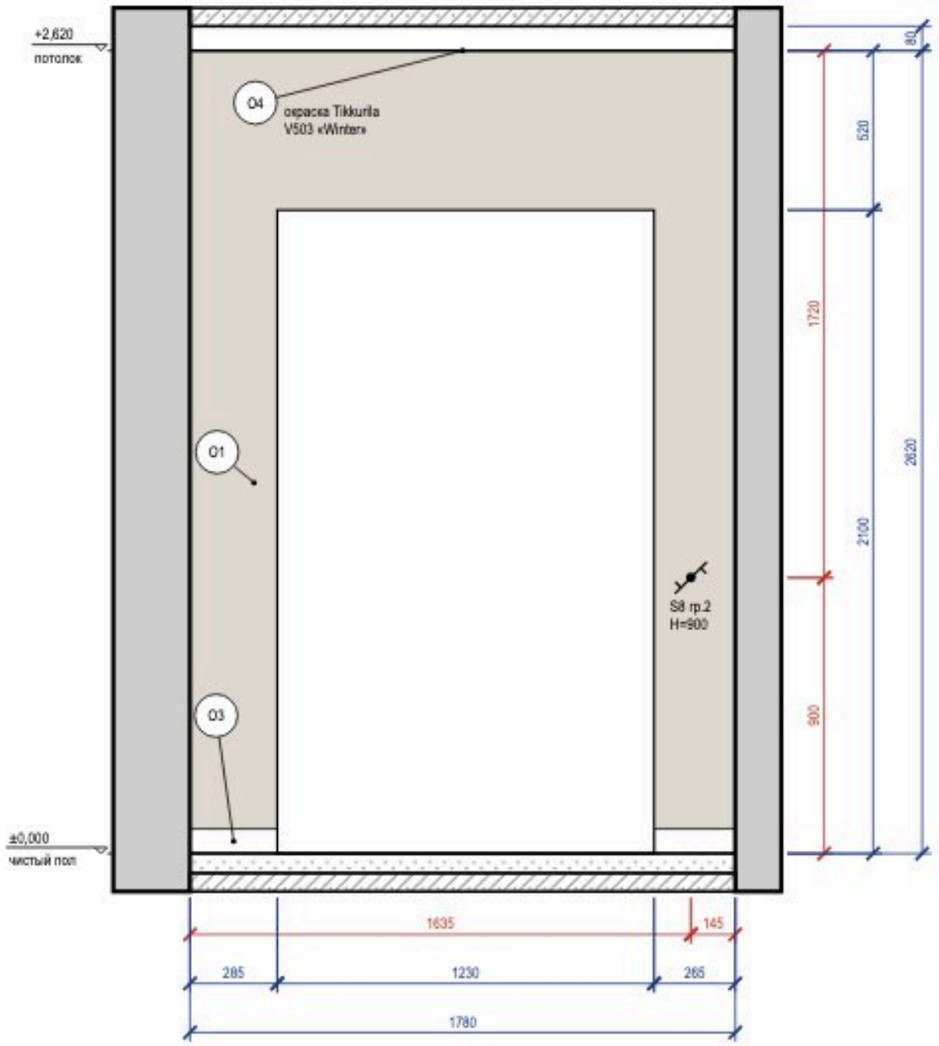



Схема развёрток (М 1:100)

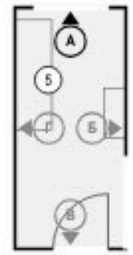

Ведомость отделки (на листе)

Марка	Поверхность	Материал, изделие	Цвет, код	Кол.
О1	стены	окраска, Farrow & Ball Modern Emulsion, матовая, подготовка Q3	Farrow & Ball No. 241 «Skimming Stone»	2,1 м²
О3	плинтус	плинтус МДФ, h 80 мм, аналог: плинтус МДФ под покраску 80×16	Farrow & Ball No. 241 «Skimming Stone»	0,6 м
О4	потолок	окраска, Tikkurila Anti-Reflex 2, глубокоматовая, подготовка Q3	Tikkurila V503 «Winter»	7,1 м²

Визуализация этой стены — лист 56

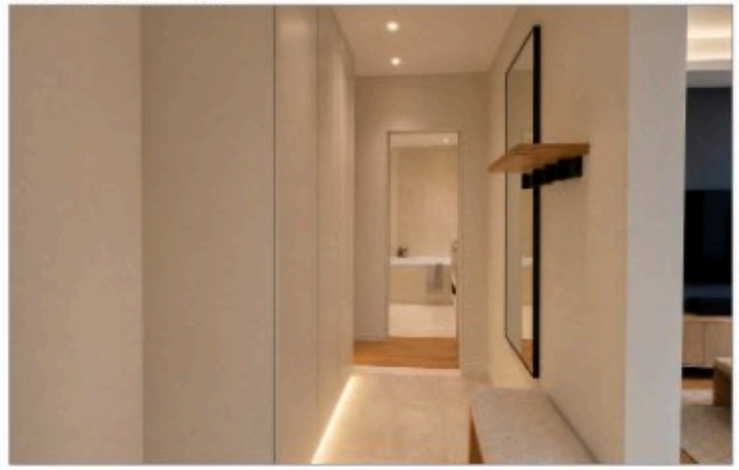

Примечания

1. Размеры — в мм от чистовых поверхностей стен; условные обозначения и общие указания — лист 2.

					Проект: Трёхкомнатная квартира
	Лист	№ док.	Подпись	Дата	
Дизайнер	Кырпан А.С.			05.10.26	Развёртка стены А. Прихожая (пом. 5)

Стадия	Лист	Листов
П	58	88

выпуск 05.10.2026 № 204f23b33a · стр. 58 из 88

Развёртка стены Б


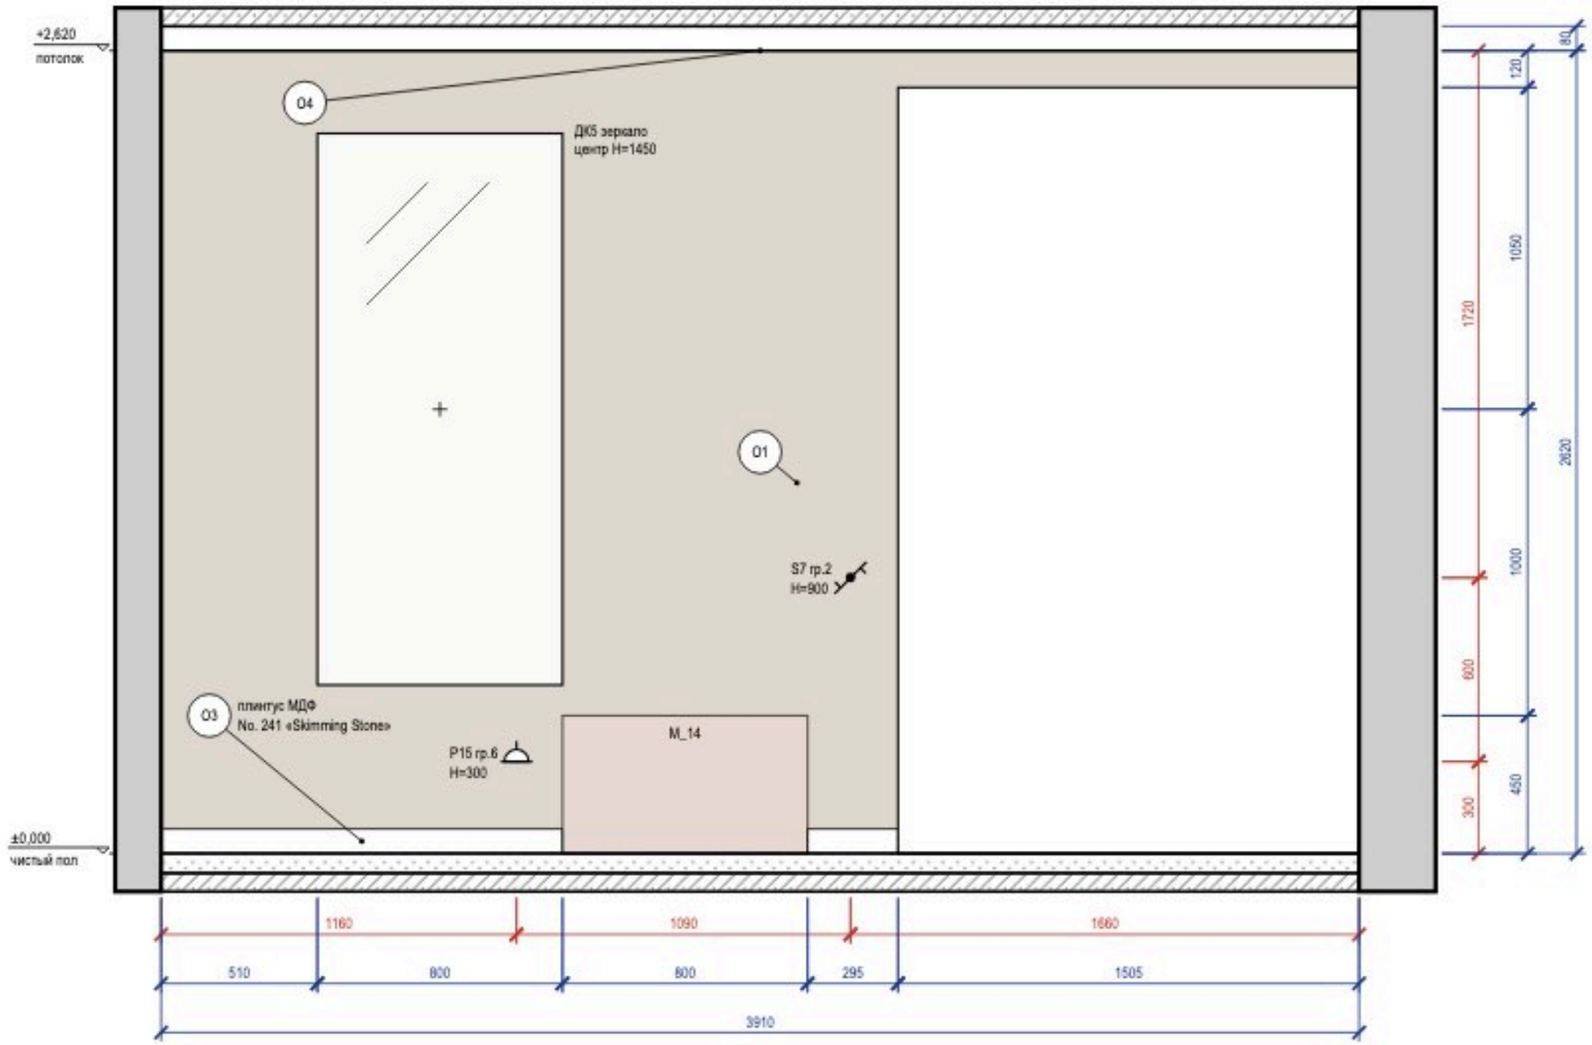



Схема развёрток (М 1:100)

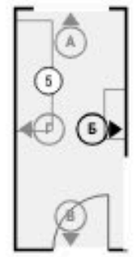

Ведомость отделки (на листе)

Марка	Поверхность	Материал, изделие	Цвет, код	Кол.
O1	стены	окраска, Farrow & Ball Modern Emulsion, матовая, подготовка Q3	Farrow & Ball No. 241 «Skimming Stone»	6,5 м²
O3	плинтус	плинтус МДФ, h 80 мм, аналог: плинтус МДФ под покраску 80×16	Farrow & Ball No. 241 «Skimming Stone»	1,6 м
O4	потолок	окраска, Tikkurila Anti-Reflex 2, глубокоматовая, подготовка Q3	Tikkurila V503 «Winter»	7,1 м²

2 **Стык покрытий пола Т-профилем без перепада (М 1:5)**
Узел 2 — лист С3

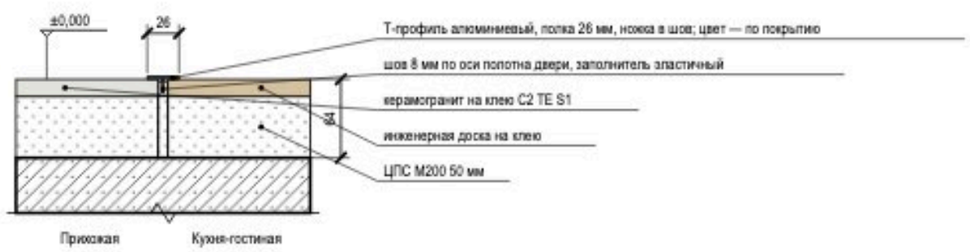

Примечания

1. Размеры — в мм от чистовых поверхностей стен; условные обозначения и общие указания — лист 2.
2. Картины и зеркала крепить к основанию по паспорту изделия (закладные и анкеры — в перечне скрытых работ); крест — ось центра предмета.

					Проект: Трёхкомнатная квартира	
	Лист	№ док.	Подпись	Дата		
Дизайнер	Кырпан А.С.			05.10.26	Развёртка стены Б. Прихожая (пом. 5)	Стадия: П; Лист: 59; Листов: 88

выпуск 05.10.2026 № 204f23b33a · стр. 59 из 88

Развёртка стены В


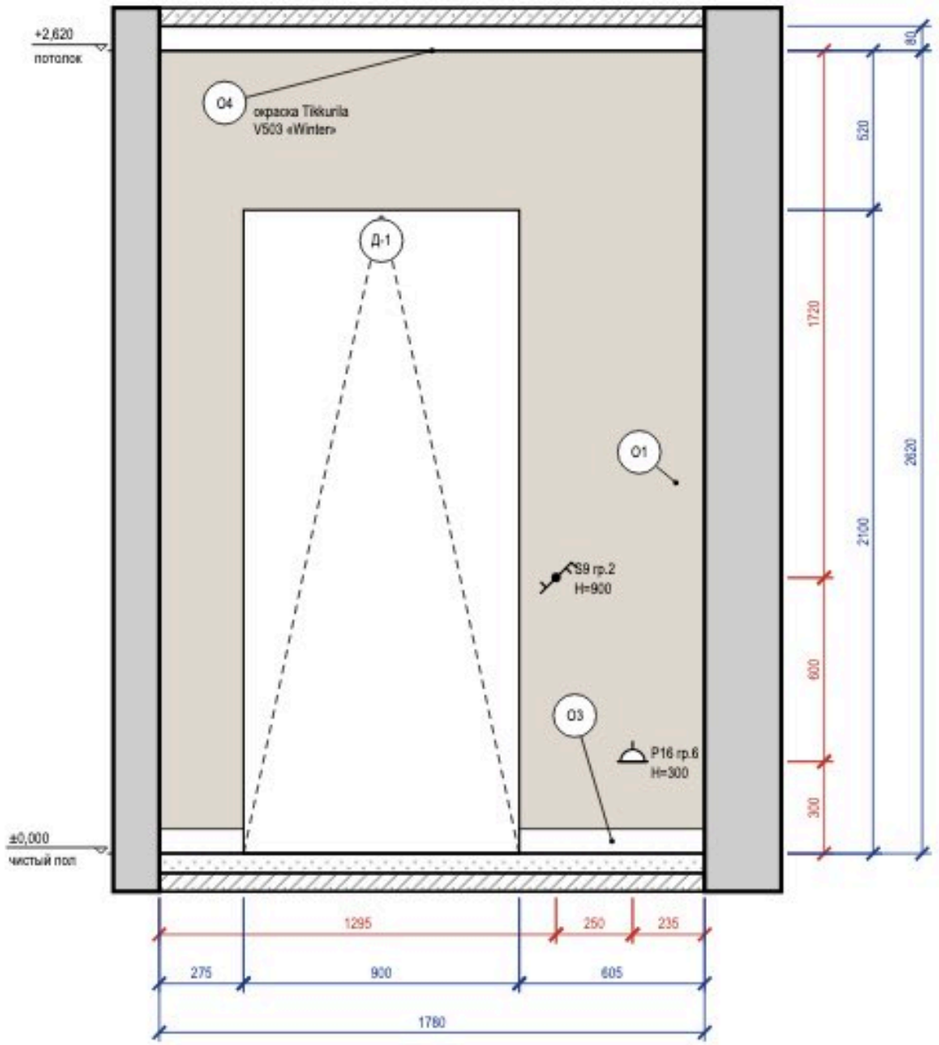



Схема развёрток (М 1:100)

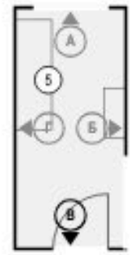

Ведомость отделки (на листе)

Марка	Поверхность	Материал, изделие	Цвет, код	Кол.
О1	стены	окраска, Farrow & Ball Modern Emulsion, матовая, подготовка Q3	Farrow & Ball No. 241 «Skimming Stone»	2,8 м²
О3	плинтус	плинтус МДФ, h 80 мм, аналог: плинтус МДФ под покраску 80×16	Farrow & Ball No. 241 «Skimming Stone»	0,9 м
О4	потолок	окраска, Tikkurila Anti-Reflex 2, глубокоматовая, подготовка Q3	Tikkurila V503 «Winter»	7,1 м²

Визуализация этой стены — лист 57

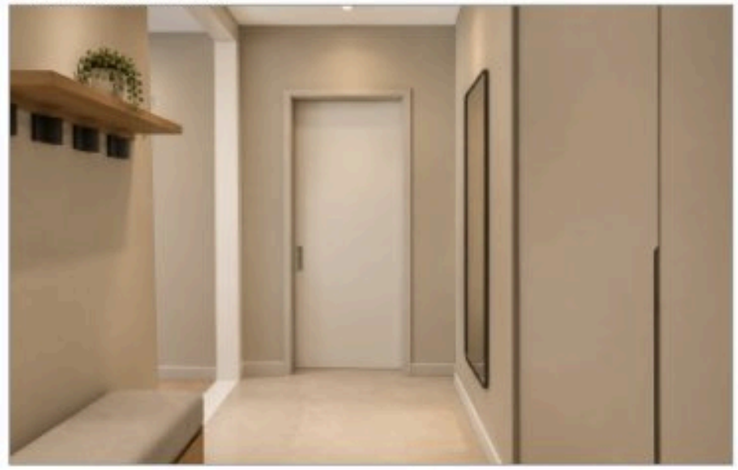

Примечания

1. Размеры — в мм от чистовых поверхностей стен; условные обозначения и общие указания — лист 2.

					Проект: Трёхкомнатная квартира
	Лист	№ док.	Подпись	Дата	Развёртка стены В. Прихожая (пом. 5)
Дизайнер	Кырпан А.С.			05.10.26	

Стадия	Лист	Листов
П	60	88

выпуск 05.10.2026 № 204f23b33a · стр. 60 из 88

Развёртка стены Г

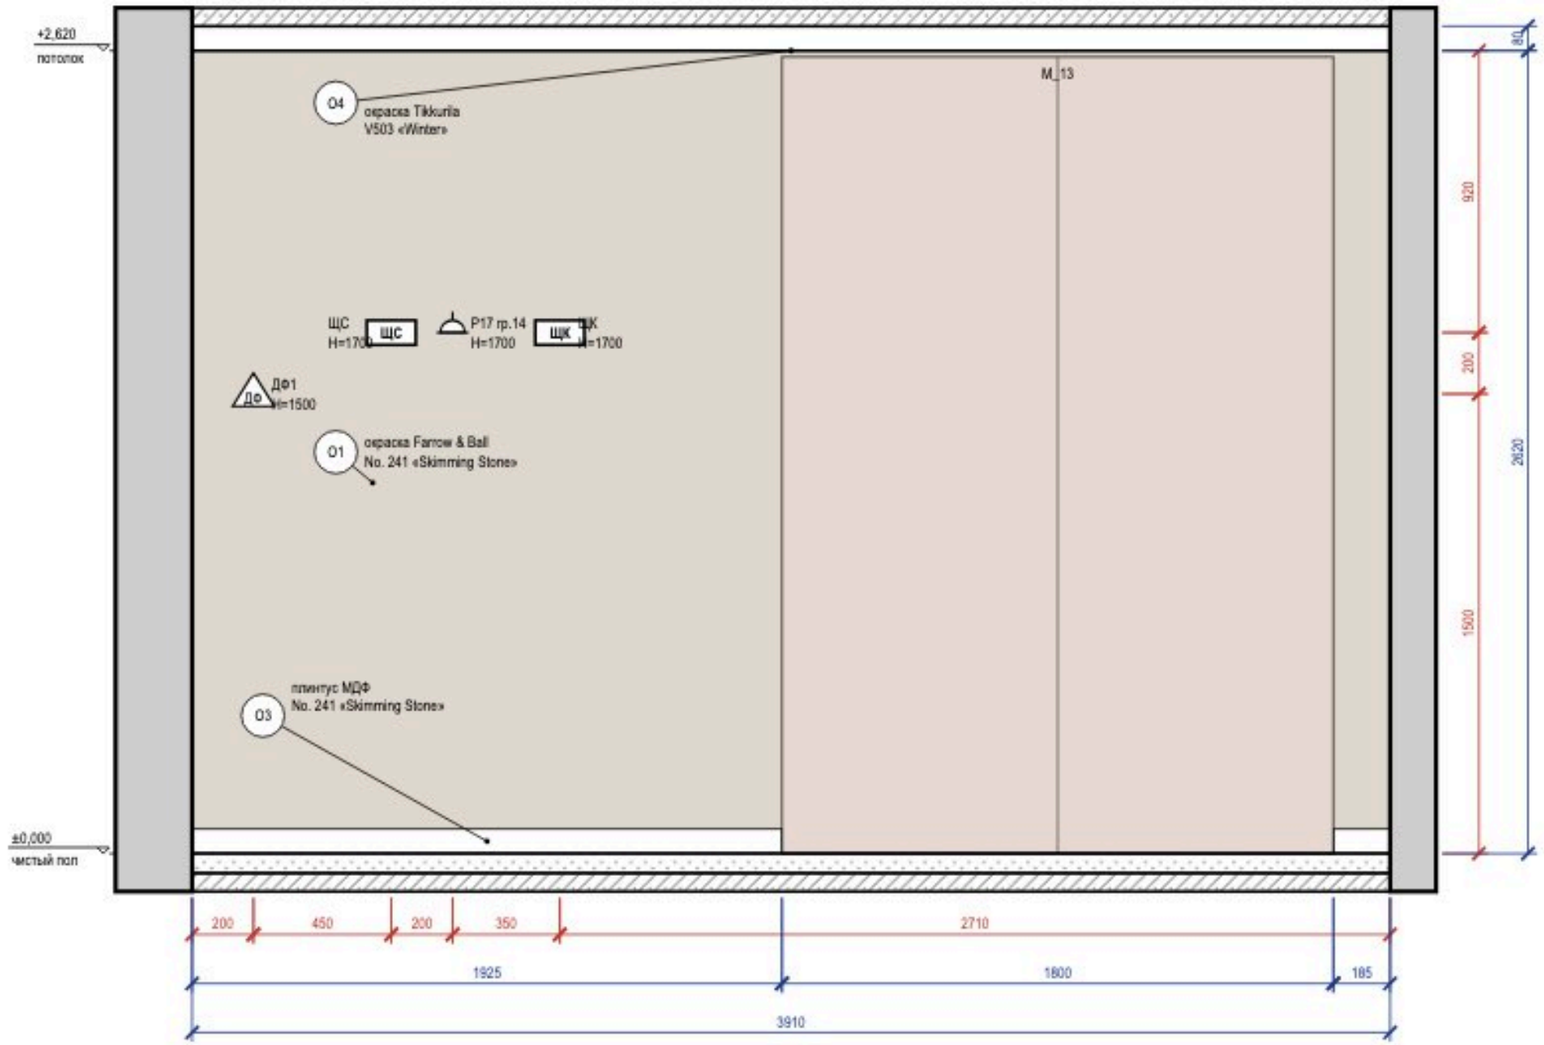


Схема развёрток (М 1:100)



Ведомость отделки (на листе)

Марка	Поверхность	Материал, изделие	Цвет, код	Кол.
О1	стены	окраска, Farrow & Ball Modern Emulsion, матовая, подготовка Q3	Farrow & Ball No. 241 «Skimming Stone»	10,2 м²
О3	плинтус	плинтус МДФ, h 80 мм, аналог: плинтус МДФ под покраску 80×16	Farrow & Ball No. 241 «Skimming Stone»	2,1 м
О4	потолок	окраска, Tikkurila Anti-Reflex 2, глубокоматовая, подготовка Q3	Tikkurila V503 «Winter»	7,1 м²

Примечания

1. Размеры — в мм от чистовых поверхностей стен; условные обозначения и общие указания — лист 2.

					Проект: Трёхкомнатная квартира
	Лист	№ док.	Подпись	Дата	Развёртка стены Г. Прихожая (пом. 5)
Дизайнер	Кырпан А.С.			05.10.26	

Стадия	Лист	Листов
П	61	88

выпуск 05.10.2026 № 204f23b33a · стр. 61 из 88



					Проект: Трёхкомнатная квартира
	Лист	№ док.	Подпись	Дата	
Дизайнер	Кырпан А.С.			05.10.26	Визуализация кухни-гостиной

Стадия	Лист	Листов
П	62	88

выпуск 05.10.2026 № 204f23b33a · стр. 62 из 88



					Проект: Трёхкомнатная квартира	
	Лист	№ док.	Подпись	Дата		
Дизайнер	Кырпан А.С.			05.10.26	Визуализация кухни-гостиной	Стадия: П; Лист: 63; Листов: 88

выпуск 05.10.2026 № 204f23b33a · стр. 63 из 88



					Проект: Трёхкомнатная квартира	
	Лист	№ док.	Подпись	Дата		
Дизайнер	Кырпан А.С.			05.10.26	Визуализация кухни-гостиной	Стадия: П; Лист: 64; Листов: 88

выпуск 05.10.2026 № 204f23b33a · стр. 64 из 88



					Проект: Трёхкомнатная квартира			
	Лист	№ док.	Подпись	Дата	Визуализация кухни-гостиной	Стадия	Лист	Листов
Дизайнер	Кырпан А.С.			05.10.26		П	65	88

выпуск 05.10.2026 № 204f23b33a · стр. 65 из 88



					Проект: Трёхкомнатная квартира	
	Лист	№ док.	Подпись	Дата	Визуализация кухни-гостиной	Стадия / Лист / Листов
Дизайнер	Кырпан А.С.			05.10.26		П / 66 / 88

выпуск 05.10.2026 № 204f23b33a · стр. 66 из 88



					Проект: Трёхкомнатная квартира
	Лист	№ док.	Подпись	Дата	
Дизайнер	Кырпан А.С.			05.10.26	Визуализация кухни-гостиной

Стадия	Лист	Листов
П	67	88

выпуск 05.10.2026 № 204f23b33a · стр. 67 из 88

Развёртка стены Б2

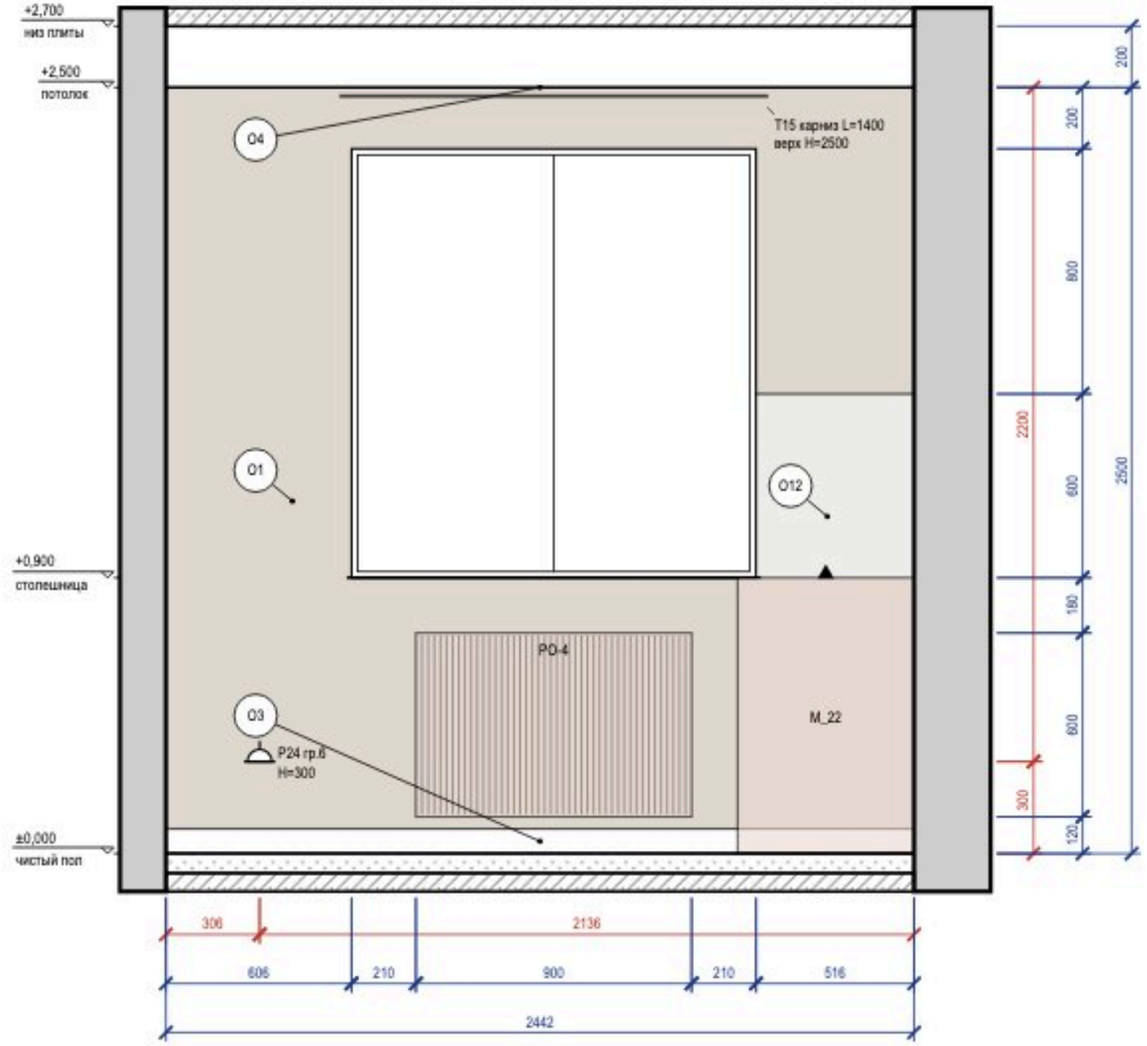


Схема развёрток (М 1:100)



Ведомость отделки (на листе)

Марка	Поверхность	Материал, изделие	Цвет, код	Кол.
О1	стены	окраска, Farrow & Ball Modern Emulsion, матовая, подготовка Q3	Farrow & Ball No. 241 «Skimming Stone»	3,9 м²
О3	плинтус	плинтус МДФ, h 80 мм, аналог: плинтус МДФ под покраску 80×16	Farrow & Ball No. 241 «Skimming Stone»	2,4 м
О4	потолок	окраска, Tikkurila Anti-Reflex 2, глубокоматовая, подготовка Q3	Tikkurila V503 «Winter»	29,2 м²
О12	фартук	керамогранит, 1200×600×9 мм, аналог: керамогранит под травертин, матовый, затирка CG2WA		0,3 м²

Примечания

1. Размеры — в мм от чистовых поверхностей стен; условные обозначения и общие указания — лист 2.
2. Карнизы (шины) — по ведомости текстиля декоратора; длина L и верх H — по развёртке, крепление — до окраски потолка.
3. Высота фартука принята 600 мм над столешницей там, где нет навесных модулей и высота фартука не задана.
4. Выводы кухонной техники — по утверждённому проекту кухни: привязки выводов даются от осей модулей гарнитура.
5. Потолок на развёртках — по нижнему уровню У1; другие уровни потолка помещения: У2 +2,600.

					Проект: Трёхкомнатная квартира
	Лист	№ док.	Подпись	Дата	Развёртка стены Б2. Кухня-гостиная (пом. 6), кухонный
Дизайнер	Кырпан А.С.			05.10.26	

Стадия	Лист	Листов
П	68	88

выпуск 05.10.2026 № 204f23b33a · стр. 68 из 88

Развёртка стены В1

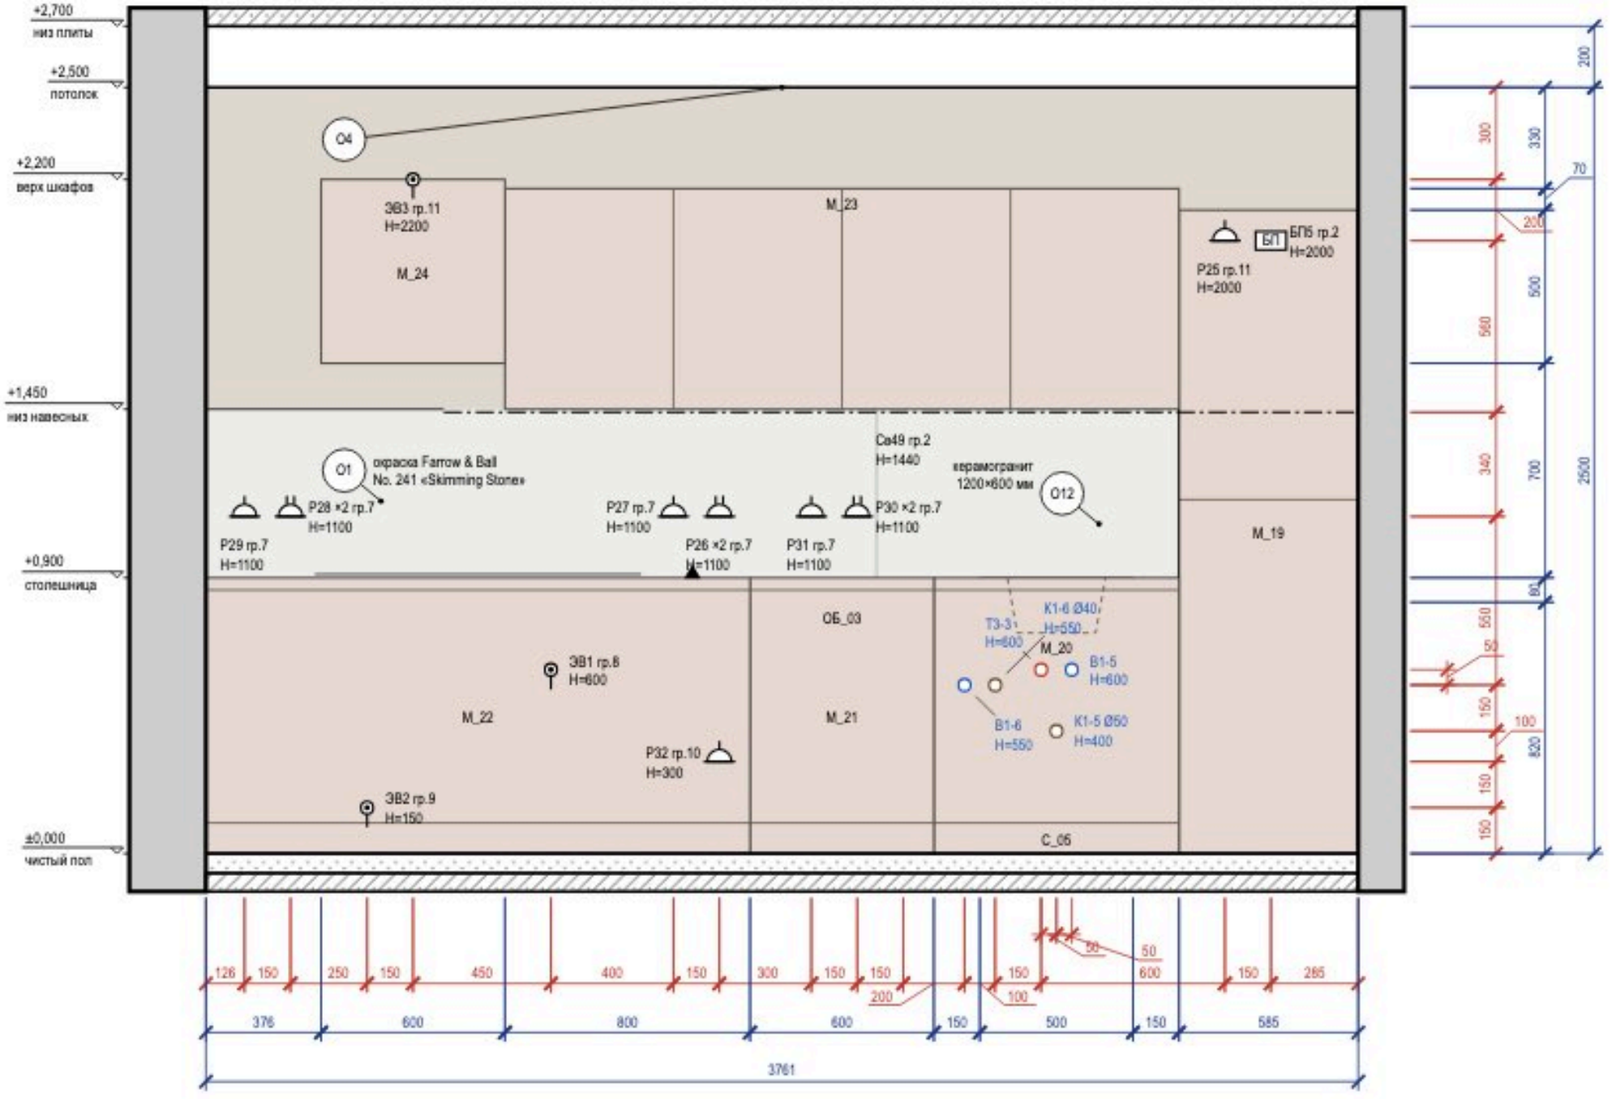


Схема развёрток (М 1:100)



Ведомость отделки (на листе)

Марка	Поверхность	Материал, изделие	Цвет, код	Кол.
О1	стены	окраска, Farrow & Ball Modern Emulsion, матовая, подготовка Q3	Farrow & Ball No. 241 «Skimming Stone»	7,7 м²
О4	потолок	окраска, Tikkurila Anti-Reflex 2, глубокоматовая, подготовка Q3	Tikkurila V503 «Winter»	29,2 м²
О12	фартук	керамогранит, 1200×600×9 мм, аналог: керамогранит под травертин, матовый, затирка CG2WA		1,7 м²

Визуализация этой стены — лист 62



Примечания

1. Размеры — в мм от чистовых поверхностей стен; условные обозначения и общие указания — лист 2.
2. Схема мебели, приборов и декора не является технической документацией для производства мебели; габариты — по паспортам изделий.
3. Выводы кухонной техники — по утверждённому проекту кухни: привязки вывода даются от осей модулей гарнитура.
4. Потолок на развёртках — по нижнему уровню У1; другие уровни потолка помещения: У2 +2,600.

					Проект: Трёхкомнатная квартира
	Лист	№ док.	Подпись	Дата	Развёртка стены В1. Кухня-гостиная (пом. 6), кухонный
Дизайнер	Кырпан А.С.			05.10.26	

Стадия	Лист	Листов
П	69	88

выпуск 05.10.2026 · 204f23b33a · стр. 69 из 88

Развёртка стены А

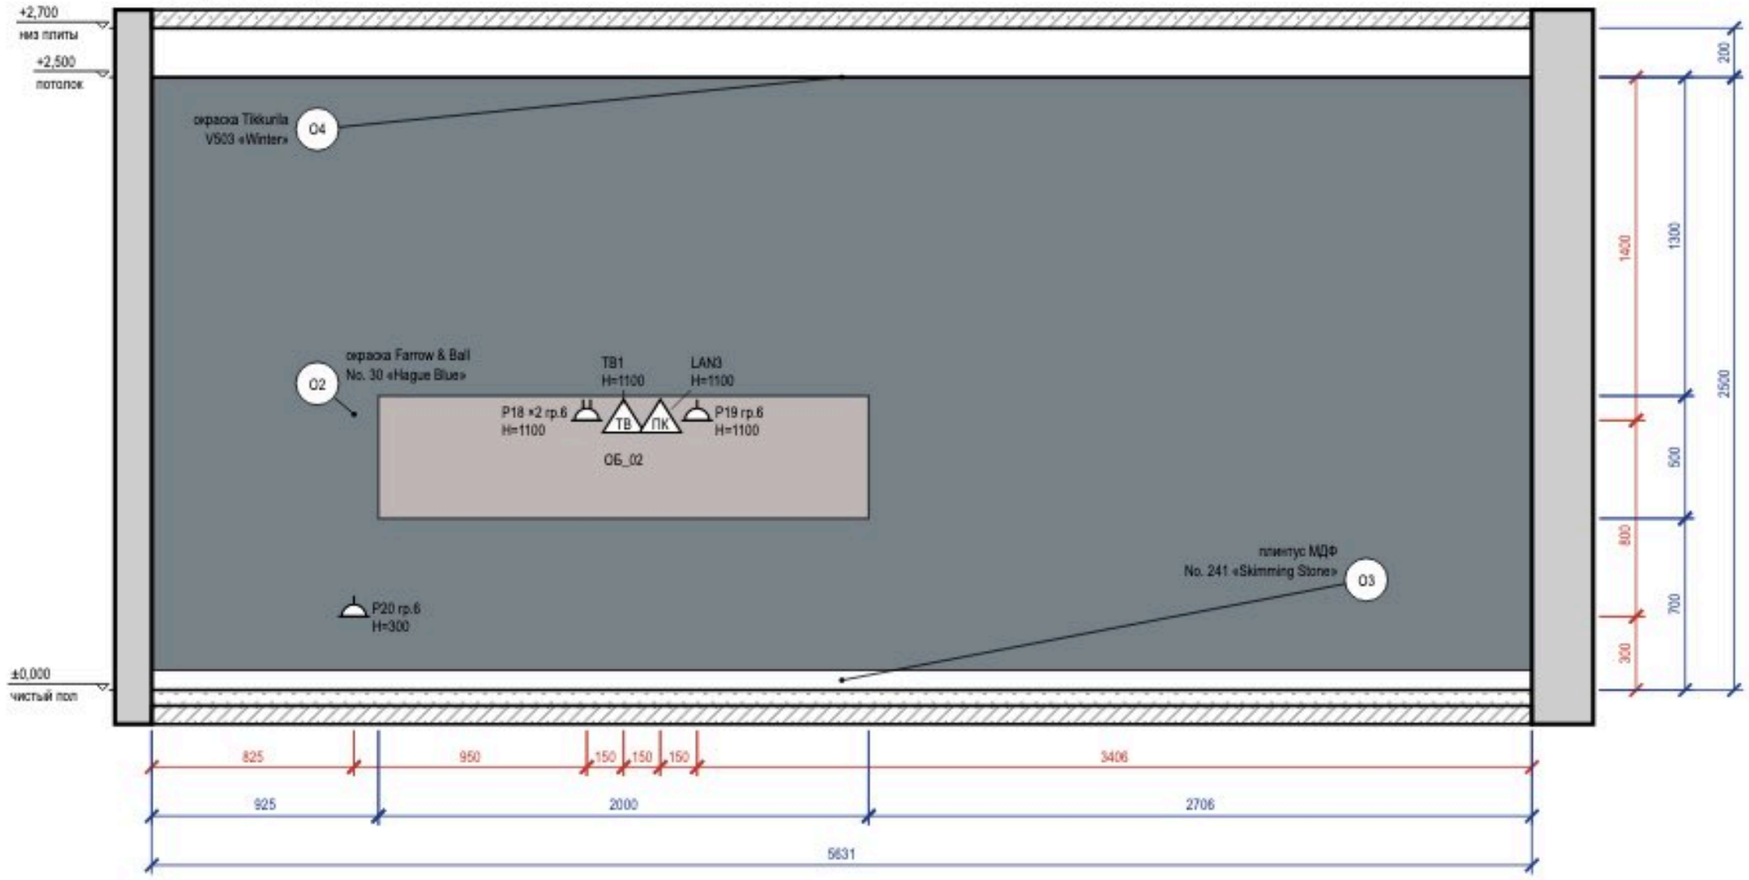


Схема развёрток (М 1:100)



Ведомость отделки (на листе)

Марка	Поверхность	Материал, изделие	Цвет, код	Кол.
О2	акцентная стена	окраска, Farrow & Ball Modern Emulsion, матовая, подготовка Q3	Farrow & Ball No. 30 «Hague Blue»	14,1 м²
О3	плинтус	плинтус МДФ, h 80 мм, аналог: плинтус МДФ под покраску 80×16	Farrow & Ball No. 241 «Skimming Stone»	5,6 м
О4	потолок	окраска, Tikkurila Anti-Reflex 2, глубокоматовая, подготовка Q3	Tikkurila V503 «Winter»	29,2 м²

Визуализация этой стены — лист 63



Примечания

1. Размеры — в мм от чистовых поверхностей стен; условные обозначения и общие указания — лист 2.
2. Схема мебели, приборов и декора не является технической документацией для производства мебели; габариты — по паспортам изделий.
3. Потолок на развёртках — по нижнему уровню У1; другие уровни потолка помещения: У2 +2,600.

					Проект: Трёхкомнатная квартира		
	Лист	№ док.	Подпись	Дата	Развёртка стены А. Кухня-гостиная (пом. 6)	Стадия	Лист	Листов
Дизайнер	Кырпан А.С.			05.10.26		П	70	88

выпуск 05.10.2026 № 204f23b33a · стр. 70 из 88

Развёртка стены Б1

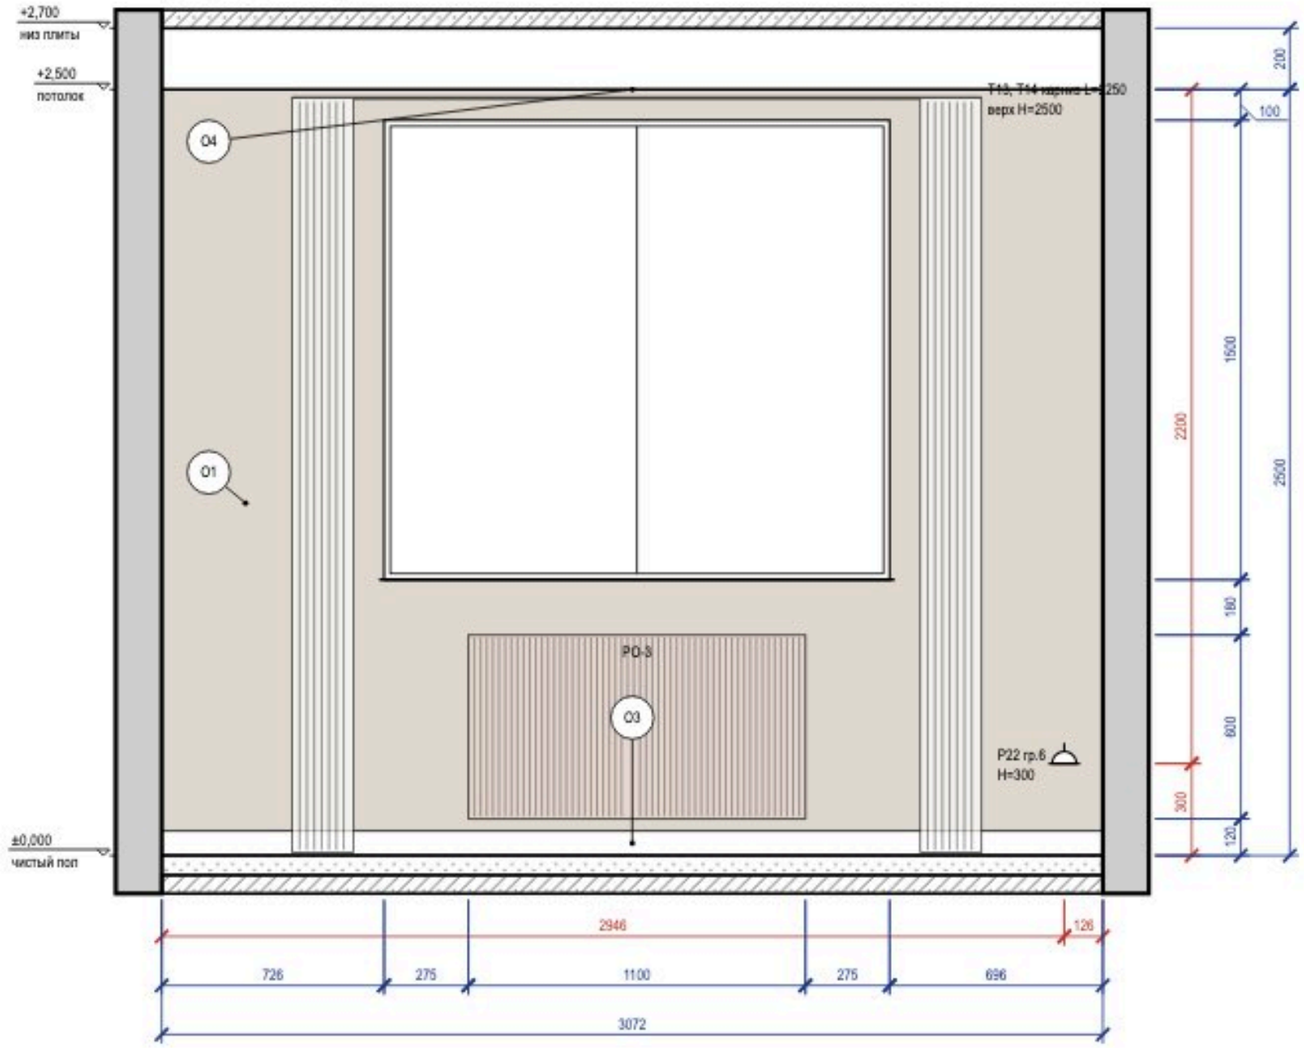


Схема развёрток (М 1:100)



Ведомость отделки (на листе)

Марка	Поверхность	Материал, изделие	Цвет, код	Кол.
О1	стены	окраска, Farrow & Ball Modern Emulsion, матовая, подготовка Q3	Farrow & Ball No. 241 «Skimming Stone»	5,2 м²
О3	плинтус	плинтус МДФ, h 80 мм, аналог: плинтус МДФ под покраску 80×16	Farrow & Ball No. 241 «Skimming Stone»	3,1 м
О4	потолок	окраска, Tikkurila Anti-Reflex 2, глубокоматовая, подготовка Q3	Tikkurila V503 «Winter»	29,2 м²

Визуализация этой стены — лист 65



Примечания


1. Размеры — в мм от чистовых поверхностей стен; условные обозначения и общие указания — лист 2.
2. Карнизы (шины) — по ведомости текстиля декоратора; длина L и верх H — по развёртке, крепление — до окраски потолка.
3. Потолок на развёртках — по нижнему уровню У1; другие уровни потолка помещения: У2 +2,600.
4. Линии узора (швы плитки, складки штор, рёбра радиаторов) прерываются у знаков и выносок — просвет между линиями не менее 0,7 мм.

					Проект: Трёхкомнатная квартира
	Лист	№ док.	Подпись	Дата	Развёртка стены Б1. Кухня-гостиная (пом. 6)
Дизайнер	Кырпан А.С.			05.10.26	

Стадия	Лист	Листов
П	71	88

выпуск 05.10.2026 № 204f23b33a · стр. 71 из 88

Развёртка стены В2

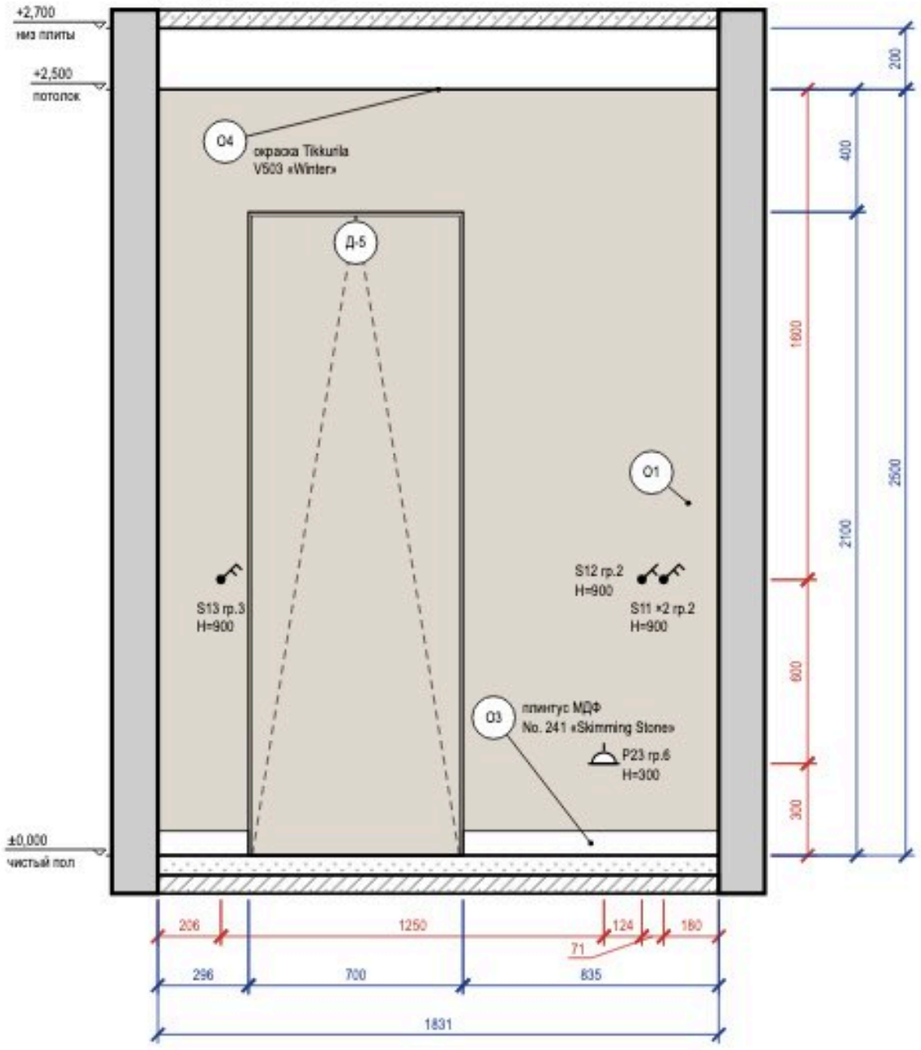

Развёртка стены Г1


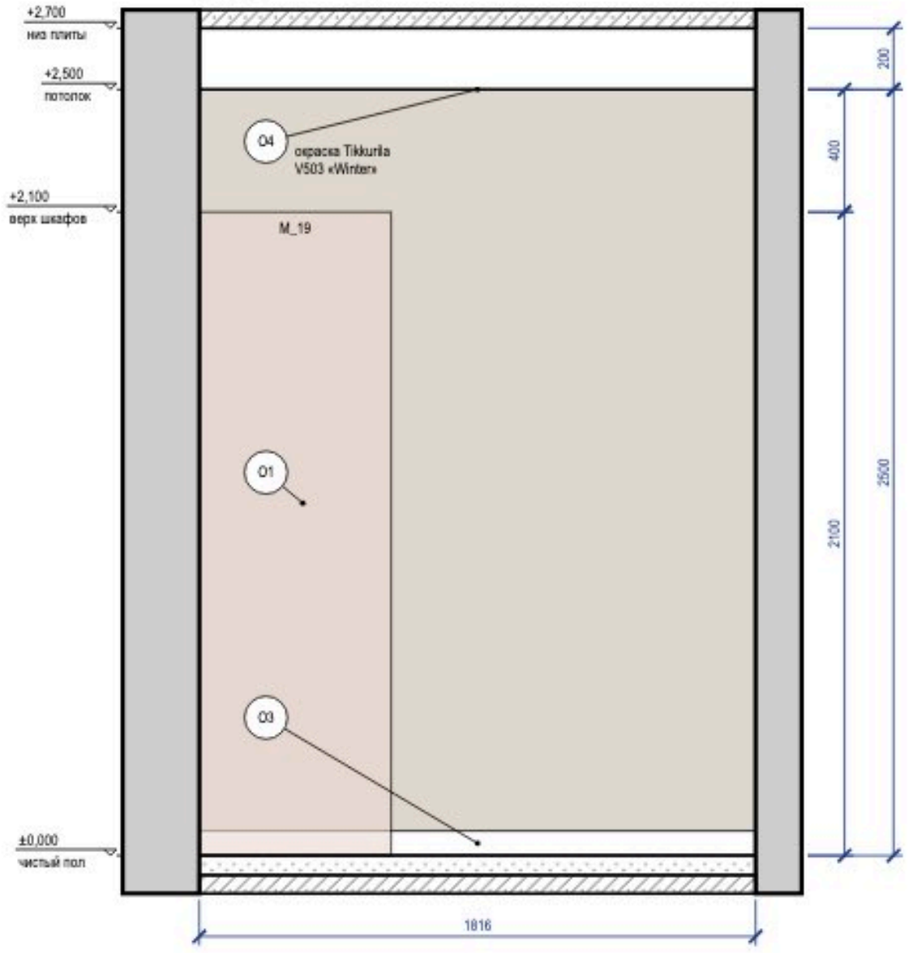



Схема развёрток (М 1:100)

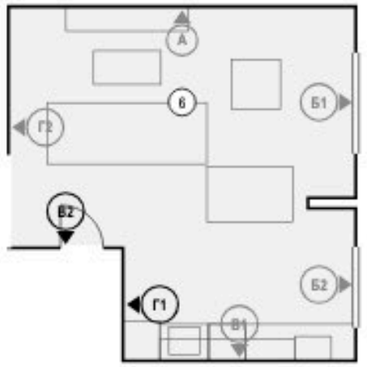

Ведомость отделки (на листе)

Марка	Поверхность	Материал, изделие	Цвет, код	Кол.
О1	стены	окраска, Farrow & Ball Modern Emulsion, матовая, подготовка Q3	Farrow & Ball No. 241 «Skimming Stone»	7,6 м²
О3	плинтус	плинтус МДФ, h 80 мм, аналог: плинтус МДФ под покраску 80×16	Farrow & Ball No. 241 «Skimming Stone»	2,9 м
О4	потолок	окраска, Tikkurila Anti-Reflex 2, глубокоматовая, подготовка Q3	Tikkurila V503 «Winter»	29,2 м²

Визуализация этой стены — лист 66

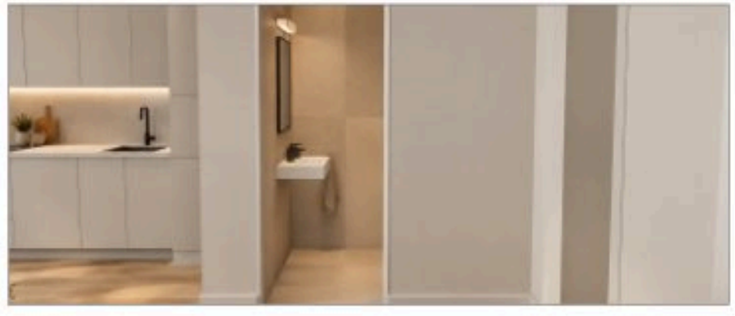

Примечания

1. Размеры — в мм от чистовых поверхностей стен; условные обозначения и общие указания — лист 2.
2. Двери скрытого монтажа — полотно в плоскости стены, отделка стены по полотну, плинтус прерывается у короба (узел — на листе узлов).
3. Потолок на развёртках — по нижнему уровню У1; другие уровни потолка помещения: У2 +2,600.

					Проект: Трёхкомнатная квартира
	Лист	№ док.	Подпись	Дата	
Дизайнер	Кырпан А.С.			05.10.26	Развёртки стен В2, Г1. Кухня-гостиная (пом. 6)
					Стадия: П; Лист: 72; Листов: 88

выпуск 05.10.2026 № 204f23b33a · стр. 72 из 88

Развёртка стены Г2

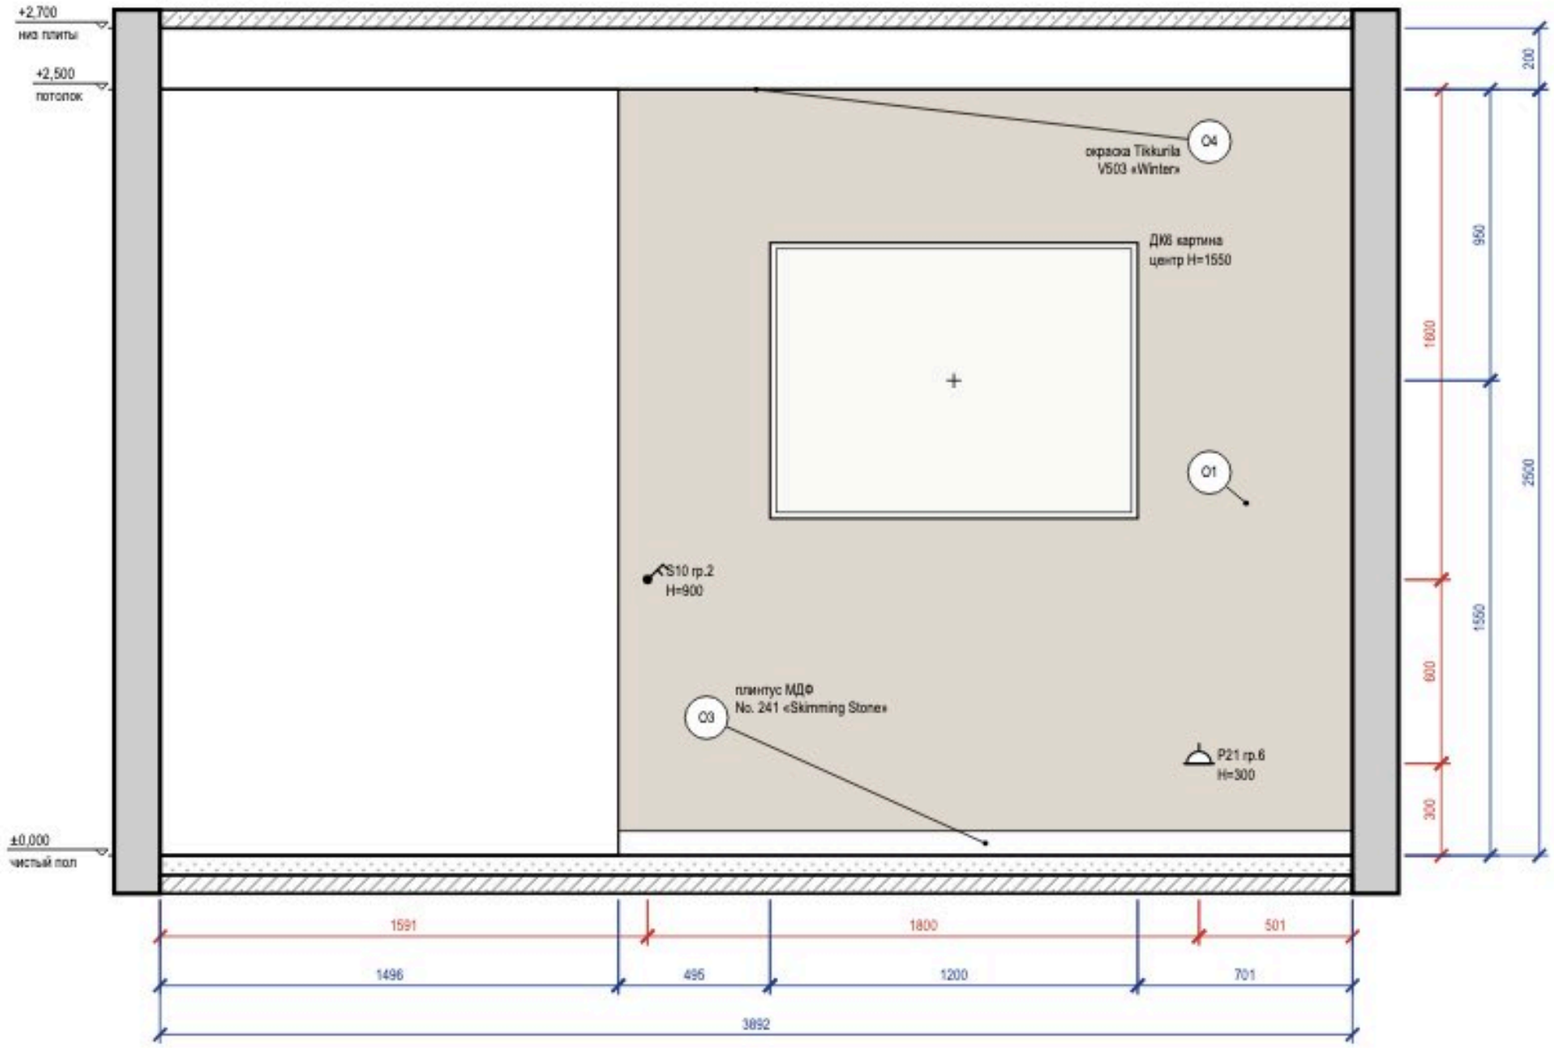


Схема развёрток (М 1:100)



Ведомость отделки (на листе)

Марка	Поверхность	Материал, изделие	Цвет, код	Кол.
О1	стены	окраска, Farrow & Ball Modern Emulsion, матовая, подготовка Q3	Farrow & Ball No. 241 «Skimming Stone»	6 м²
О3	плинтус	плинтус МДФ, h 80 мм, аналог: плинтус МДФ под покраску 80×16	Farrow & Ball No. 241 «Skimming Stone»	2,4 м
О4	потолок	окраска, Tikkurila Anti-Reflex 2, глубокоматовая, подготовка Q3	Tikkurila V503 «Winter»	29,2 м²

Визуализация этой стены — лист 64



Примечания

1. Размеры — в мм от чистовых поверхностей стен; условные обозначения и общие указания — лист 2.
2. Картины и зеркала крепить к основанию по паспорту изделия (закладные и анкеры — в перечне скрытых работ); крест — ось центра предмета.
3. Потолок на развёртках — по нижнему уровню У1; другие уровни потолка помещения: У2 +2,600.

	Лист	№ док.	Подпись	Дата
Дизайнер	Кырпан А.С.			05.10.26

Проект: Трёхкомнатная квартира

Развёртка стены Г2. Кухня-гостиная (пом. 6)

Стадия	Лист	Листов
П	73	88

выпуск 05.10.2026 № 204f23b33a · стр. 73 из 88



					Проект: Трёхкомнатная квартира	
	Лист	№ док.	Подпись	Дата		
Дизайнер	Кырпан А.С.			05.10.26	Визуализация: Санузел 2	Стадия: П; Лист: 74; Листов: 88


выпуск 05.10.2026 № 204f23b33a · стр. 74 из 88




					Проект: Трёхкомнатная квартира	
	Лист	№ док.	Подпись	Дата	Визуализация: Санузел 2	Стадия / Лист / Листов
Дизайнер	Кырпан А.С.			05.10.26		П / 75 / 88

выпуск 05.10.2026 № 204f23b33a · стр. 75 из 88

Развёртка стены А

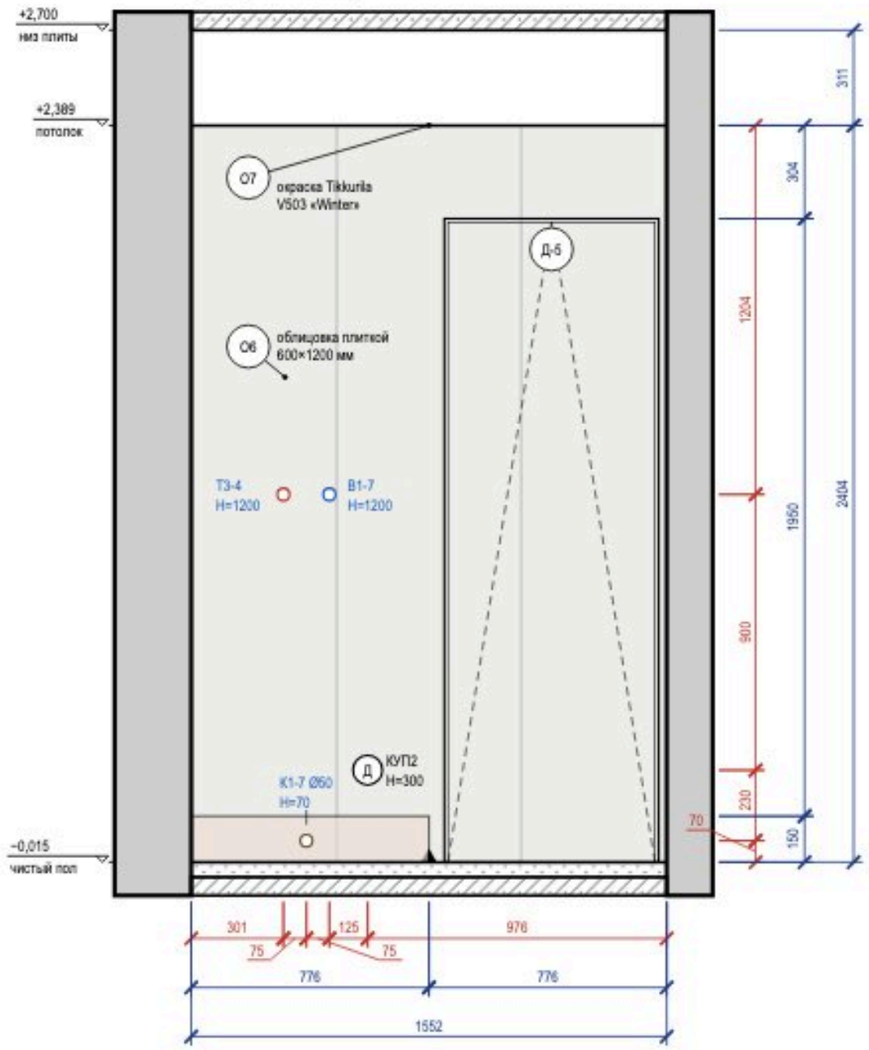

Развёртка стены Б

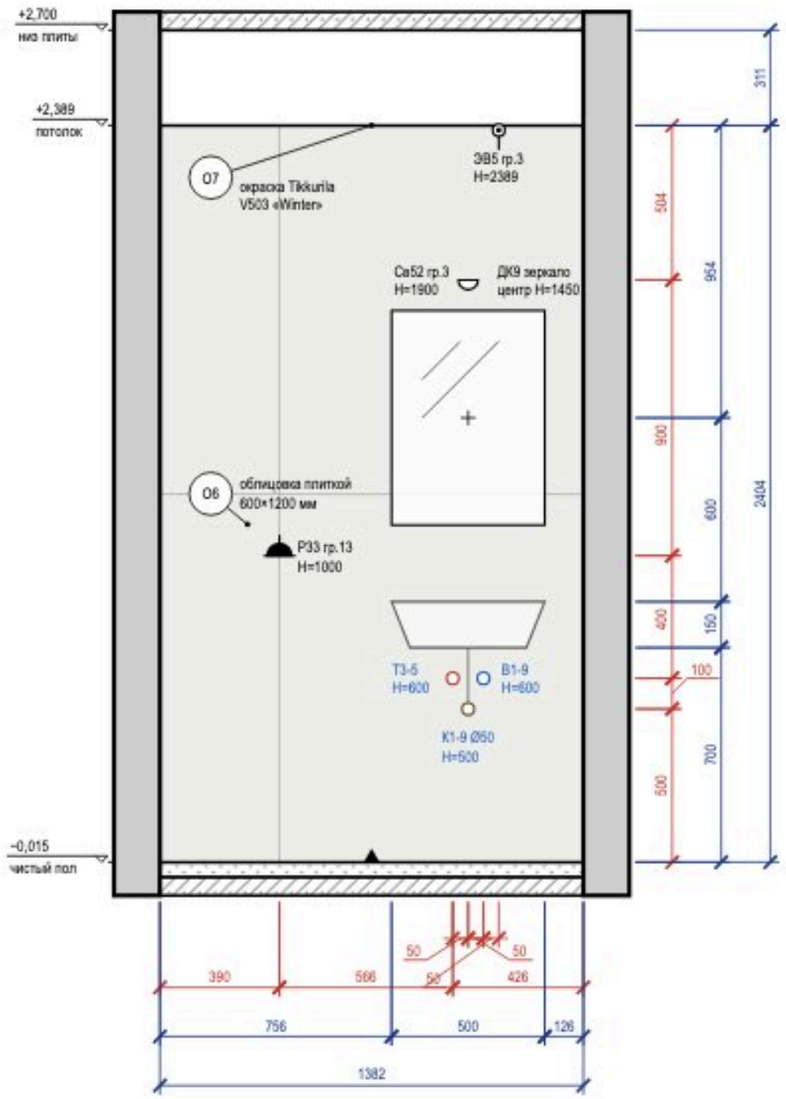

Визуализация этой стены — лист 74



Схема развёрток (М 1:100)



Ведомость отделки (на листе)

Марка	Поверхность	Материал, изделие	Цвет, код	Кол.
О6	стены	облицовка плиткой, 600×1200×9 мм, аналог: керамогранит под травертин, матовый, затирка CG2WA		5,6 м²
О7	потолок	окраска, Tikkurila Luja 7, матовая, подготовка Q3	Tikkurila V503 «Winter»	2,3 м²

Примечания

1. Размеры — в мм от чистовых поверхностей стен; условные обозначения и общие указания — лист 2.
2. Схема мебели, приборов и декора не является технической документацией для производства мебели; габариты — по паспортам изделий.
3. Выводы ВК — коды и высоты по листу выводов сантехники.
4. Облицовка — по сетке швов 2 мм, раскладка от оси стены (треугольник у пола), целые ряды от пола; подрезки — по листу раскладки плитки.
5. Гидроизоляция в 2 слоя, заход на стены 200 мм — до облицовки, с актом скрытых работ и тестом проливом (узел — на листе узлов).
6. Картины и зеркала крепить к основанию по паспорту изделия (закладные и анкеры — в перечне скрытых работ); крест — ось центра предмета.
7. Двери скрытого монтажа — полотно в плоскости стены, отделка стены по полотну, плинтус прерывается у короба (узел — на листе узлов).

	Лист	№ док.	Подпись	Дата
Дизайнер	Кырпан А.С.			05.10.26


Проект: Трёхкомнатная квартира

Развёртки стен А, Б. Санузел 2 (пом. 7)


Стадия	Лист	Листов
П	76	88

выпуск 05.10.2026 № 204f23b33a · стр. 76 из 88

Развёртка стены В

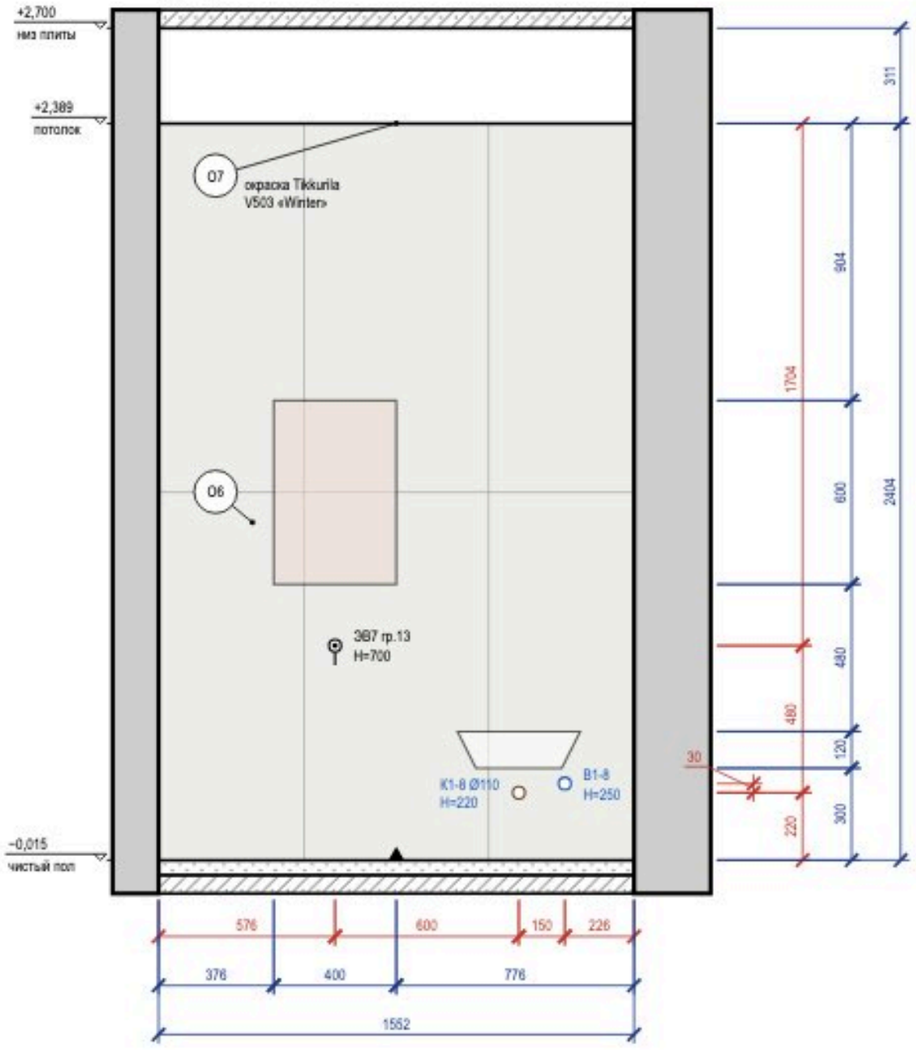

Развёртка стены Г

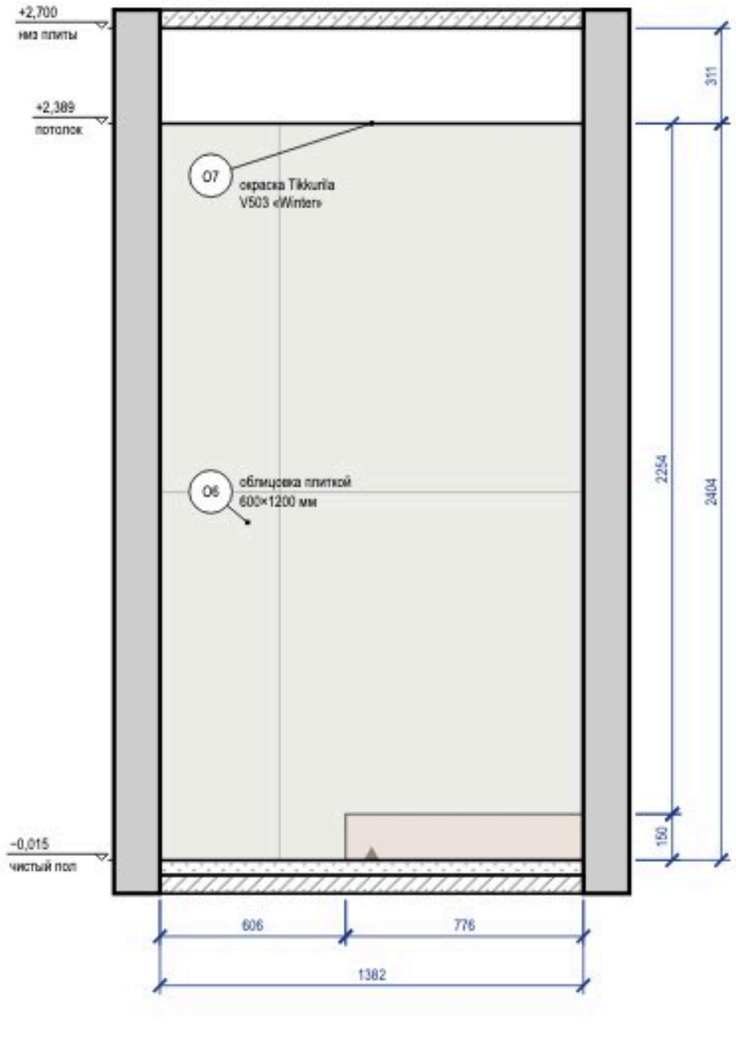

Визуализация этой стены — лист 75



Схема развёрток (М 1:100)



Ведомость отделки (на листе)

Марка	Поверхность	Материал, изделие	Цвет, код	Кол.
О6	стены	облицовка плиткой, 600×1200×9 мм, аналог: керамогранит под травертин, матовый, затирка CG2WA		7,1 м²
О7	потолок	окраска, Tikkurila Luja 7, матовая, подготовка Q3	Tikkurila V503 «Winter»	2,3 м²

Примечания

1. Размеры — в мм от чистовых поверхностей стен; условные обозначения и общие указания — лист 2.
2. Схема мебели, приборов и декора не является технической документацией для производства мебели; габариты — по паспортам изделий.
3. Выводы ВК — коды и высоты по листу выводов сантехники.
4. Облицовка — по сетке швов 2 мм, раскладка от оси стены (треугольник у пола); целые ряды от пола; подрезки — по листу раскладки плитки.
5. Гидроизоляция в 2 слоя, заход на стены 200 мм — до облицовки, с актом скрытых работ и тестом проливом (узел — на листе узлов).

					Проект: Трёхкомнатная квартира
	Лист	№ док.	Подпись	Дата	Развёртки стен В, Г. Санузел 2 (пом. 7)
Дизайнер	Кырпан А.С.			05.10.26	

Стадия	Лист	Листов
П	77	88

выпуск 05.10.2026 · 204f23b33a · стр. 77 из 88



					Проект: Трёхкомнатная квартира	
	Лист	№ док.	Подпись	Дата		
Дизайнер	Кырпан А.С.			05.10.26	Визуализация коридора	Стадия / Лист / Листов
						П / 78 / 88


выпуск 05.10.2026 № 204f23b33a · стр. 78 из 88



					Проект: Трёхкомнатная квартира	
	Лист	№ док.	Подпись	Дата		
Дизайнер	Кырпан А.С.			05.10.26	Визуализация коридора	Стадия: П; Лист: 79; Листов: 88

выпуск 05.10.2026 № 204f23b33a · стр. 79 из 88

Развёртка стены А

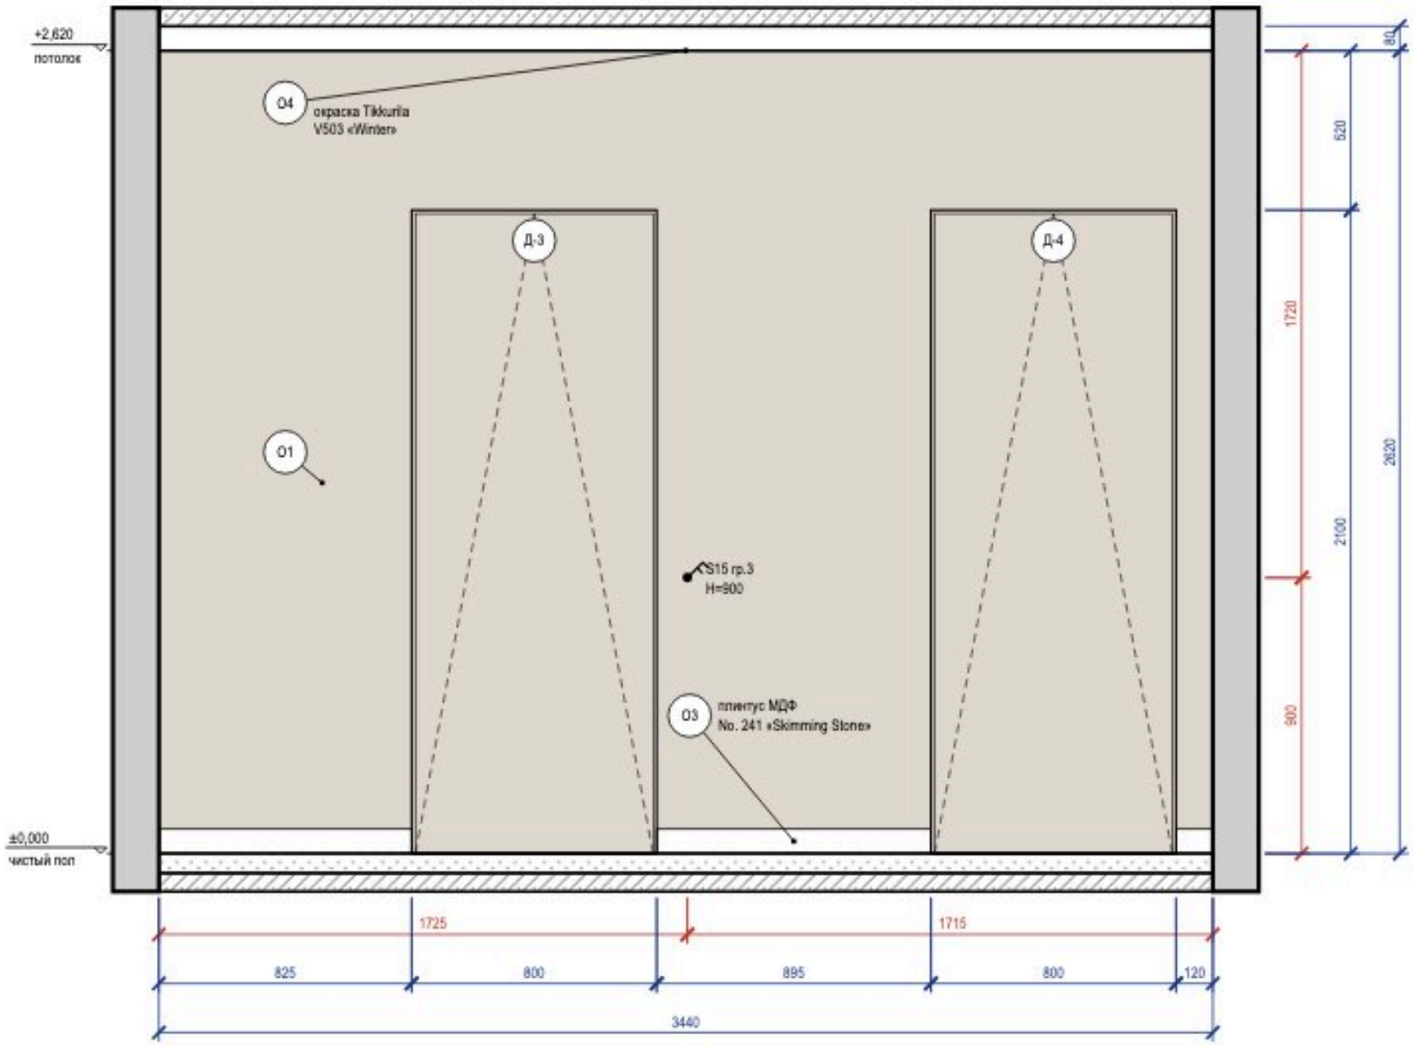

Развёртка стены Б

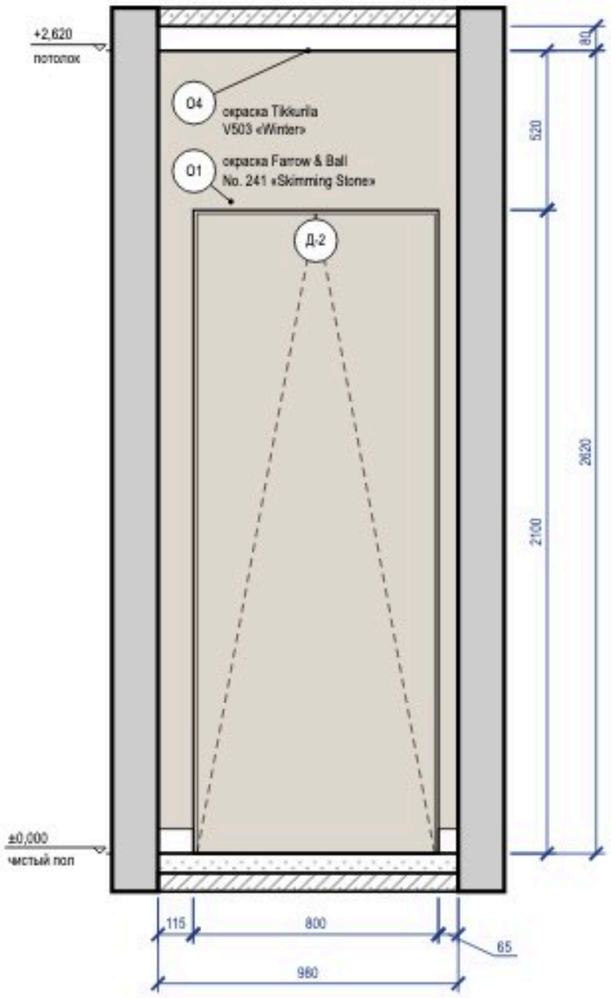



Схема развёрток (М 1:100)



Ведомость отделки (на листе)

Марка	Поверхность	Материал, изделие	Цвет, код	Кол.
О1	стены	окраска, Farrow & Ball Modern Emulsion, матовая, подготовка Q3	Farrow & Ball No. 241 «Skimming Stone»	6,5 м²
О3	плинтус	плинтус МДФ, h 80 мм, аналог: плинтус МДФ под покраску 80×16	Farrow & Ball No. 241 «Skimming Stone»	2 м
О4	потолок	окраска, Tikkurila Anti-Reflex 2, глубокоматовая, подготовка Q3	Tikkurila V503 «Winter»	3,5 м²

Визуализация этой стены — лист 78

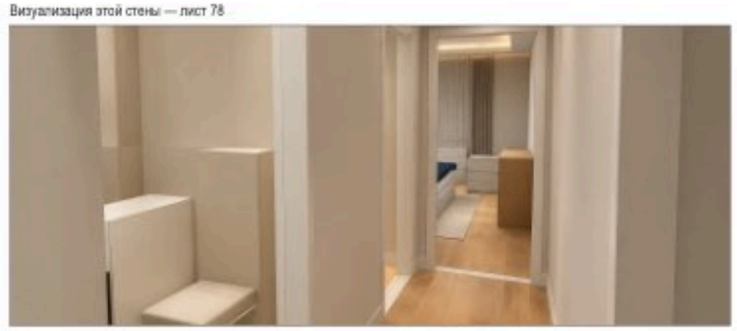

Примечания


1. Размеры — в мм от чистовых поверхностей стен; условные обозначения и общие указания — лист 2.
2. Двери скрытого монтажа — полотно в плоскости стены, отделка стены по полотну, плинтус прерывается у короба (узел — на листе узлов).

					Проект: Трёхкомнатная квартира
	Лист	№ док.	Подпись	Дата	Развёртки стен А, Б. Коридор (пом. 8)
Дизайнер	Кырпан А.С.			05.10.26	

Стадия	Лист	Листов
П	80	88

выпуск 05.10.2026 № 204f23b33a · стр. 80 из 88

Развёртка стены В

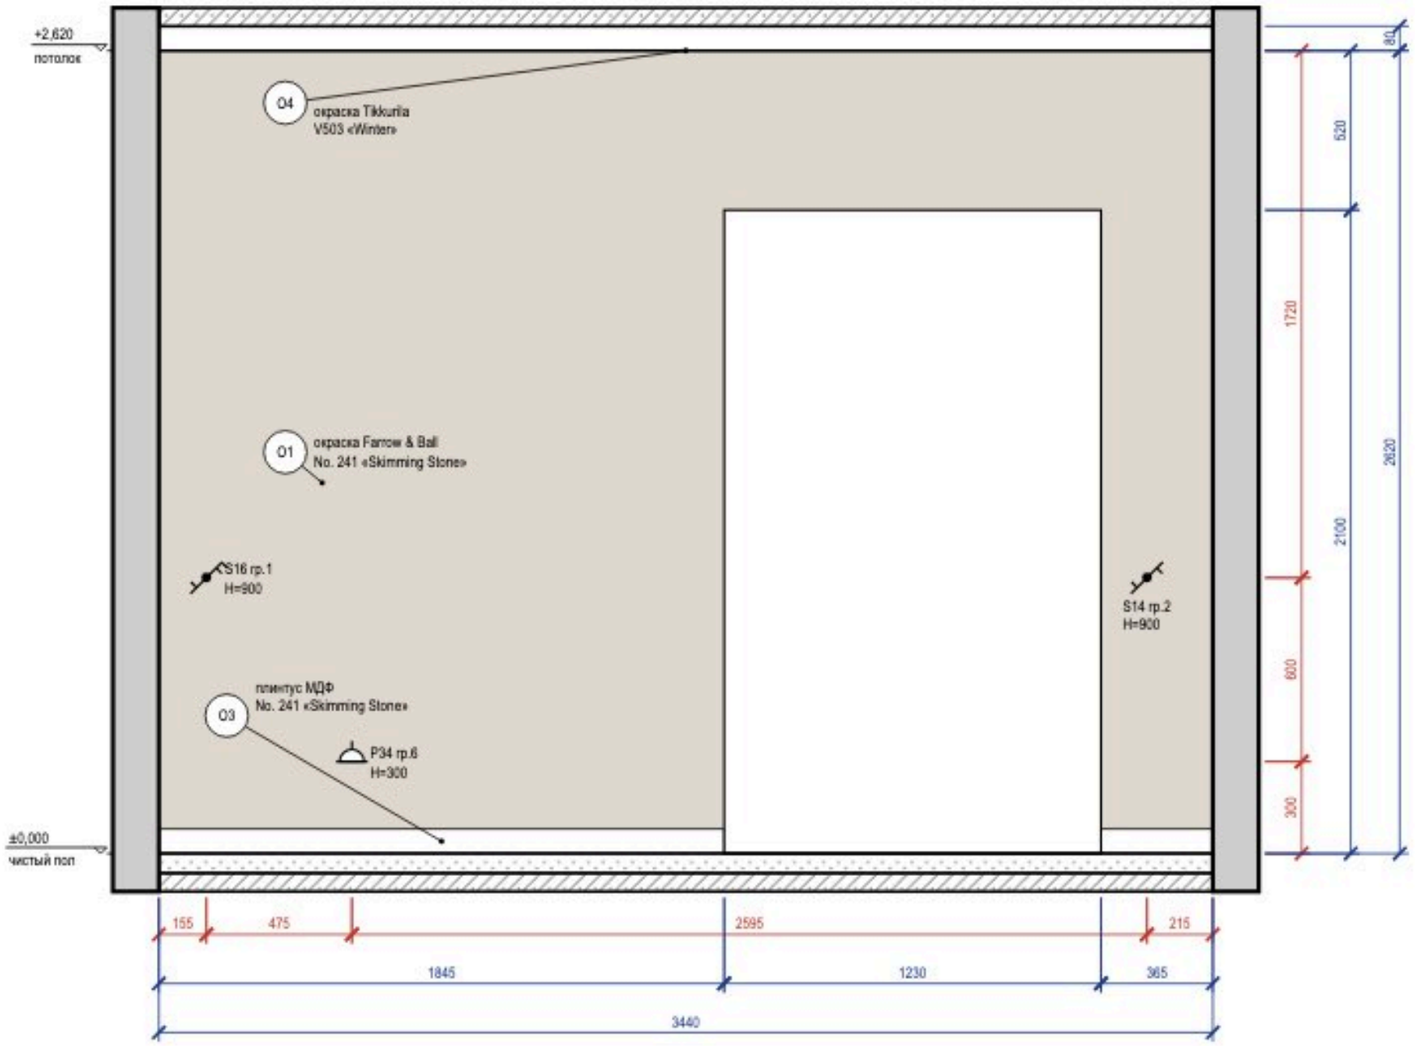

Развёртка стены Г

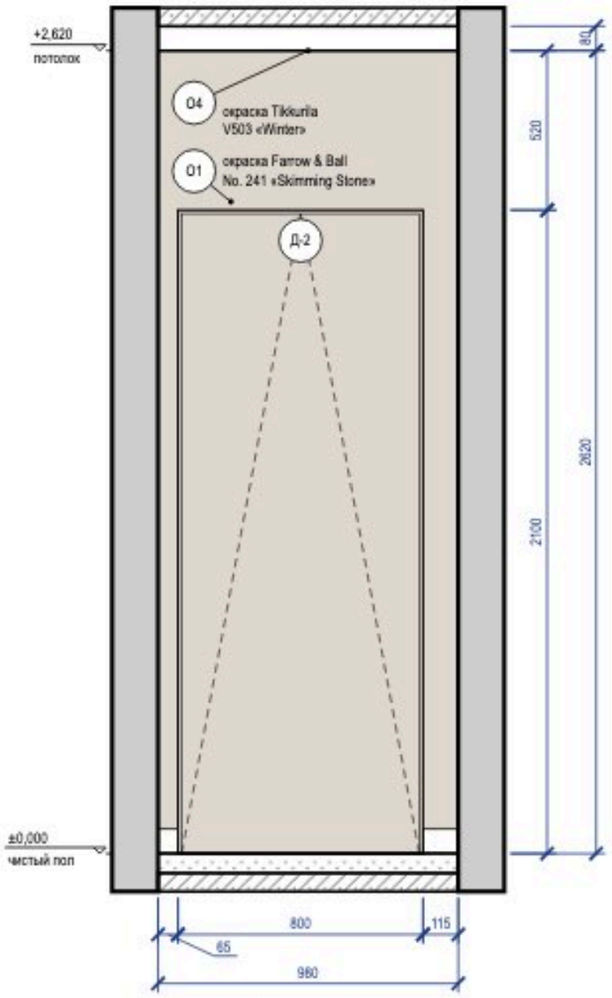



Схема развёрток (М 1:100)



Ведомость отделки (на листе)

Марка	Поверхность	Материал, изделие	Цвет, код	Кол.
О1	стены	окраска, Farrow & Ball Modern Emulsion, матовая, подготовка Q3	Farrow & Ball No. 241 «Skimming Stone»	7,3 м²
О3	плинтус	плинтус МДФ, h 80 мм, аналог: плинтус МДФ под покраску 80×16	Farrow & Ball No. 241 «Skimming Stone»	2,4 м
О4	потолок	окраска, Tikkurila Anti-Reflex 2, глубокоматовая, подготовка Q3	Tikkurila V503 «Winter»	3,5 м²

Визуализация этой стены — лист 79

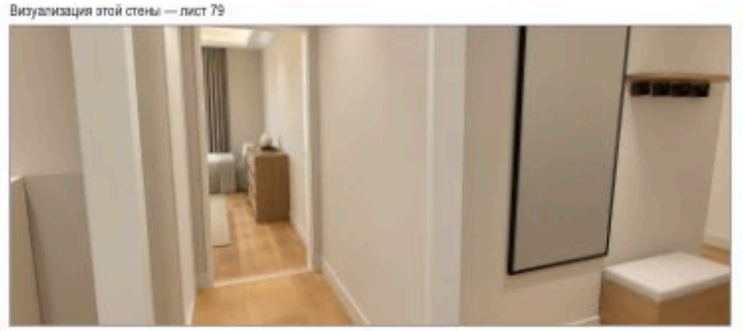

Примечания


1. Размеры — в мм от чистовых поверхностей стен; условные обозначения и общие указания — лист 2.
2. Двери скрытого монтажа — полотно в плоскости стены, отделка стены по полотну, плинтус прерывается у короба (узел — на листе узлов).

					Проект: Трёхкомнатная квартира
	Лист	№ док.	Подпись	Дата	Развёртки стен В, Г. Коридор (пом. 8)
Дизайнер	Кырпан А.С.			05.10.26	


Стадия	Лист	Листов
П	81	88

выпуск 05.10.2026 № 204f23b33a · стр. 81 из 88


Вид с фасадами

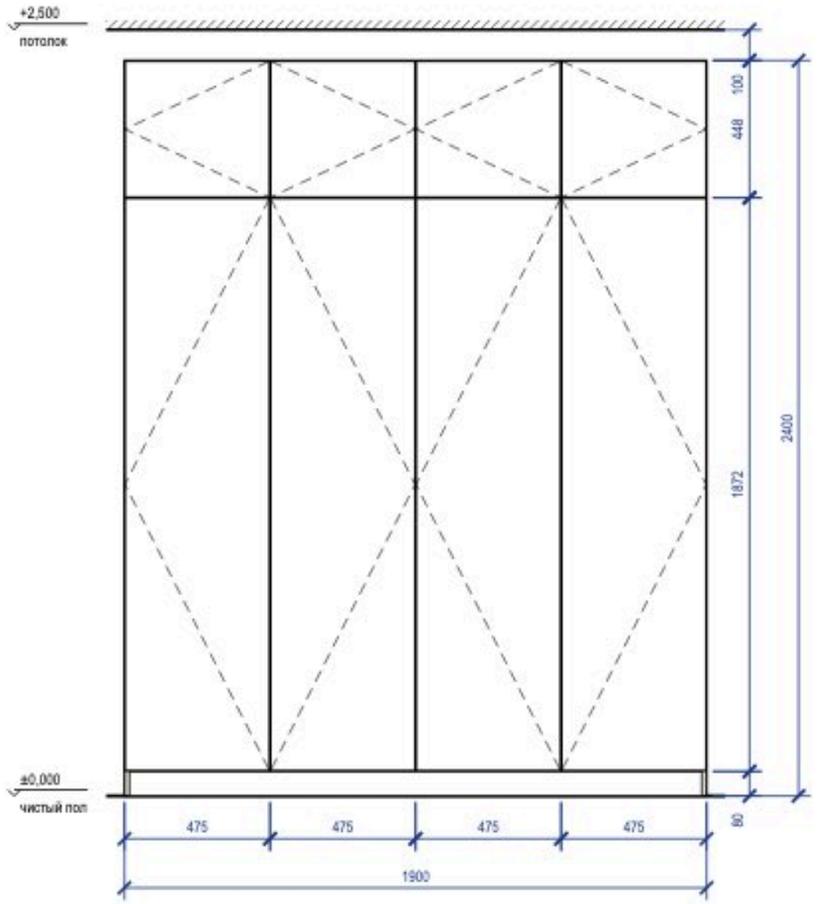


Вид без фасадов

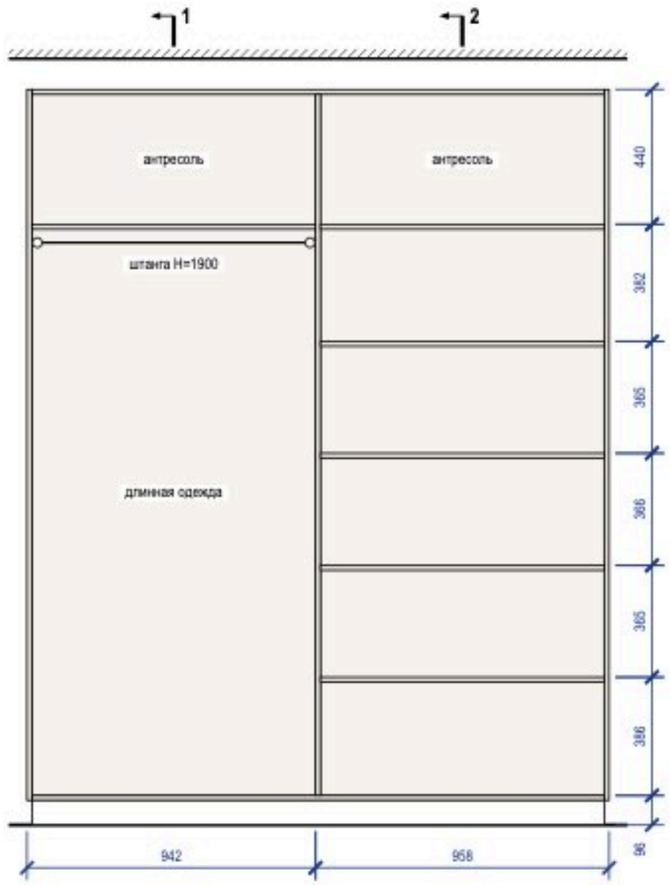

Разрез 1-1

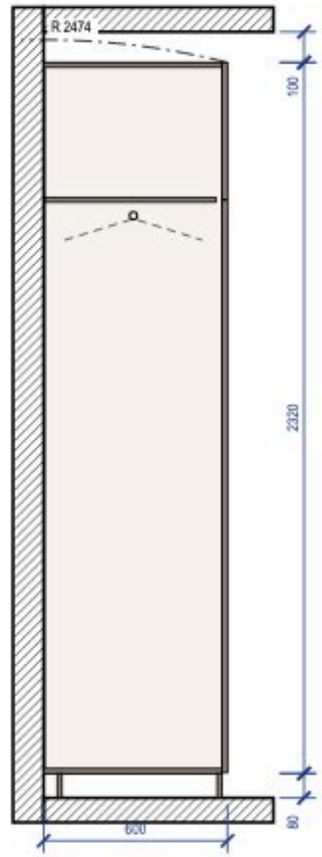


Разрез 2-2

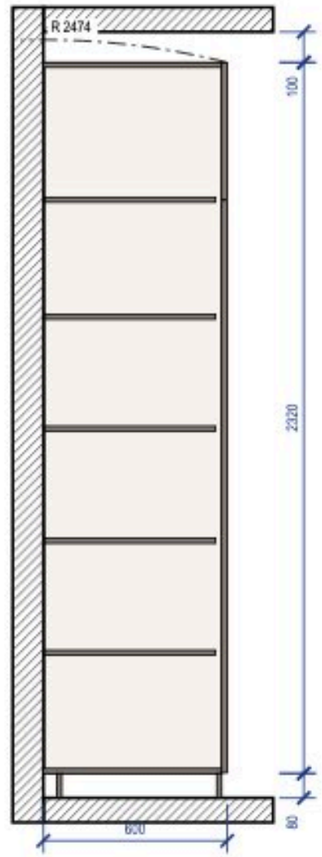

Примечания

1. Размеры — в мм по чистовой отделке; изделие 1900×600×2400 (Ш×Г×В). Перед раскроем — контрольный замер цеха после чистовой отделки стен, пола и потолка.
2. Корпус — ЛДСП 16 мм, задняя стенка ХДФ 4 мм в паз, цоколь 80 мм на регулируемых опорах; фасады — МДФ, эмаль матовая 18 мм накладные, цвет — по колерной карте; петли с доводчиком: фасад 1869 мм — 4 петли, фасад 445 мм — 2 петли.
3. Кромка: скрытые торцы 0,4 мм, видимые 2 мм (ПВХ/АБС).
4. Номинальные зазоры: между фасадами 3 мм, фасад — стена и фасад — потолок не менее 3 мм, фасад ящика — стойка 2 мм.
5. Ящики — направляющие полного выдвижения NL 550 (внутренняя глубина 578 мм ≥ NL + 3); присадка по 32-й системе — выполняет цех.
6. Зазор до потолка 100 мм — закрыть планкой в цвет корпуса при монтаже.
7. Подъём корпуса: диагональ боковины $\sqrt{(2400^2 + 600^2)} = 2474$ мм < 2500 мм до потолка — корпус собирается лёжа и поднимается поворотом.
8. Крепление к стене от опрокидывания: уголок к стене, 2 шт.; основание стены и шаг анкеров — монтажная схема шкафов.


3D орто

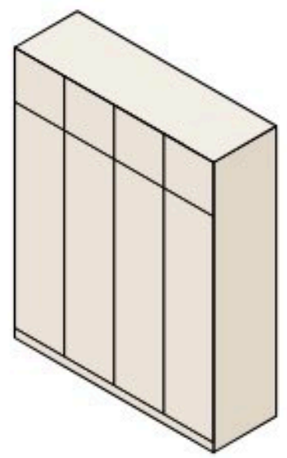


					Проект: Трёхкомнатная квартира			
	Лист	№ док.	Подпись	Дата	Шкаф распашной M_05	Стадия	Лист	Листов
Дизайнер	Кырпан А.С.			05.10.26		П	Д_1	88

выпуск 05.10.2026 № 204f23b33a · стр. 82 из 88


Общий вид

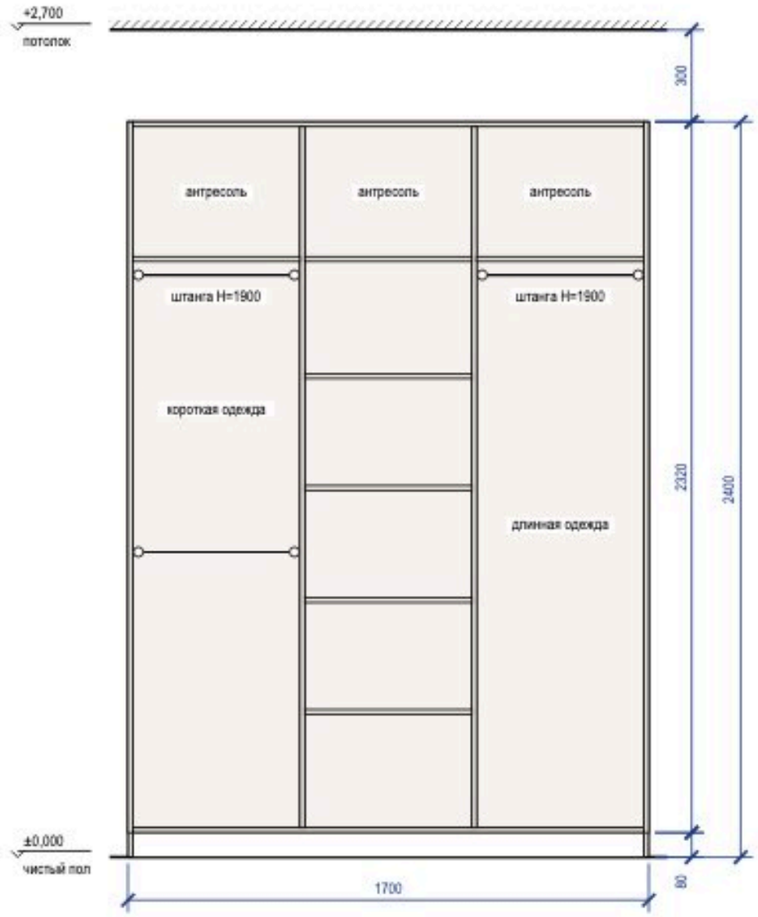


Наполнение, размеры в свету

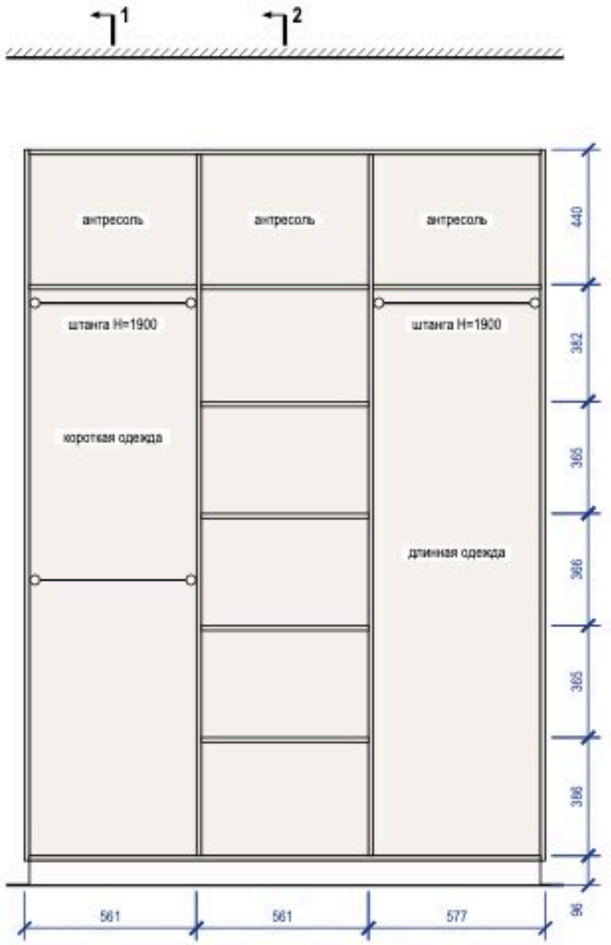

Разрез 1-1

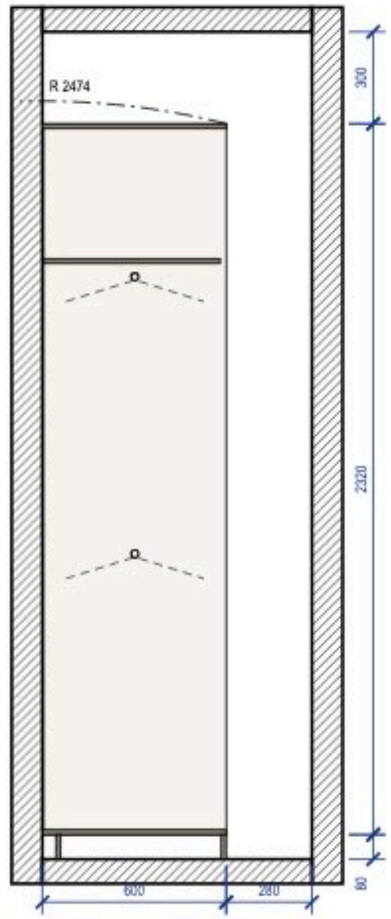


Разрез 2-2

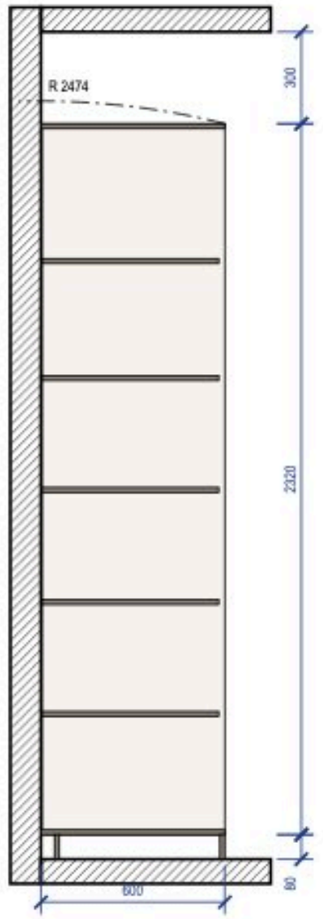

Примечания

1. Размеры — в мм по чистовой отделке; изделие 1700×600×2400 (Ш×Г×В). Перед раскроем — контрольный замер цеха после чистовой отделки стен, пола и потолка.
2. Корпус — ЛДСП 16 мм, задняя стенка ХДФ 4 мм в паз, цоколь 80 мм на регулируемых опорах; открытая система без фасадов, ящики с фасадами.
3. Кромка: скрытые торцы 0,4 мм, видимые 2 мм (ПВХ/АБС).
4. Номинальные зазоры: между фасадами ящиков 3 мм, фасад ящика — стойка 2 мм.
5. Ящики — направляющие полного выдвижения NL 550 (внутренняя глубина 596 мм ≥ NL + 3); присадка по 32-й системе — выполняет цех.
6. Зазор до потолка 300 мм.
7. Подъём корпуса: диагональ боковины $\sqrt{(2400^2 + 600^2)} = 2474$ мм < 2700 мм до потолка — корпус собирается лёжа и поднимается поворотом.
8. Крепление к стене от опрокидывания: крепление к стене, 3 точки; основание стены и шаг анкеров — монтажная схема шкафов.
9. Проход перед изделием 280 мм показан на разрезе 1-1: меньше 600 мм — глубину уменьшить (торцевые штанги при глубине 350–450 мм) или изменить расстановку.

3D орто

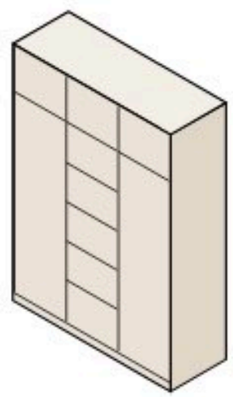


					Проект: Трёхкомнатная квартира
	Лист	№ док.	Подпись	Дата	
Дизайнер	Кырпан А.С.			05.10.26	Система хранения M_07


Стадия	Лист	Листов
П	Д_2	88

выпуск 05.10.2026 № 204f23b33a · стр. 83 из 88


Вид с фасадами

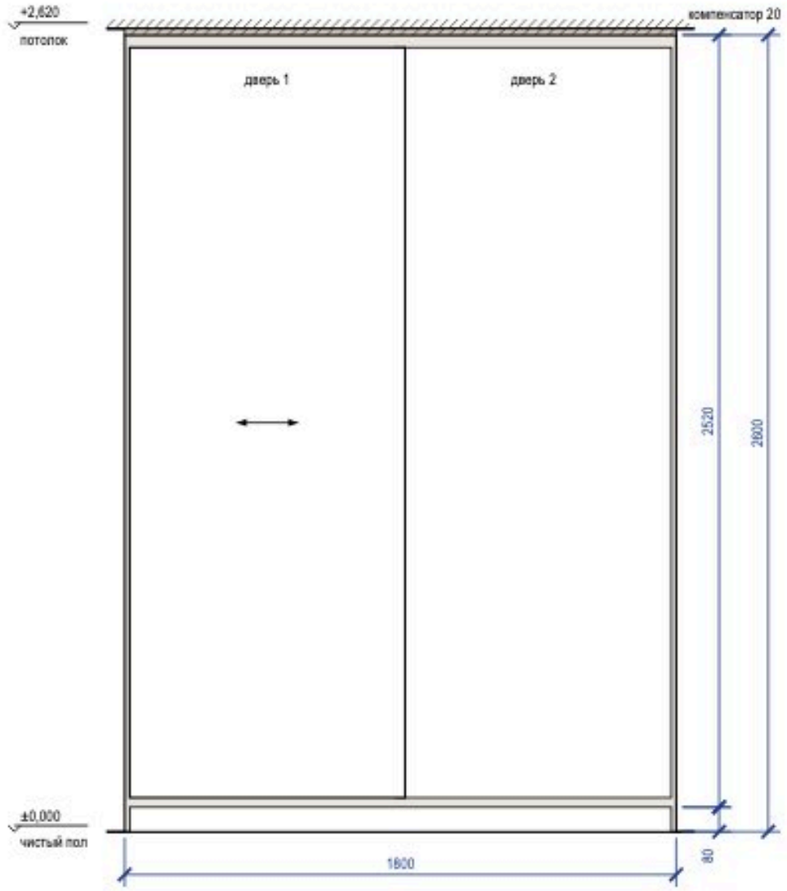


Вид без фасадов

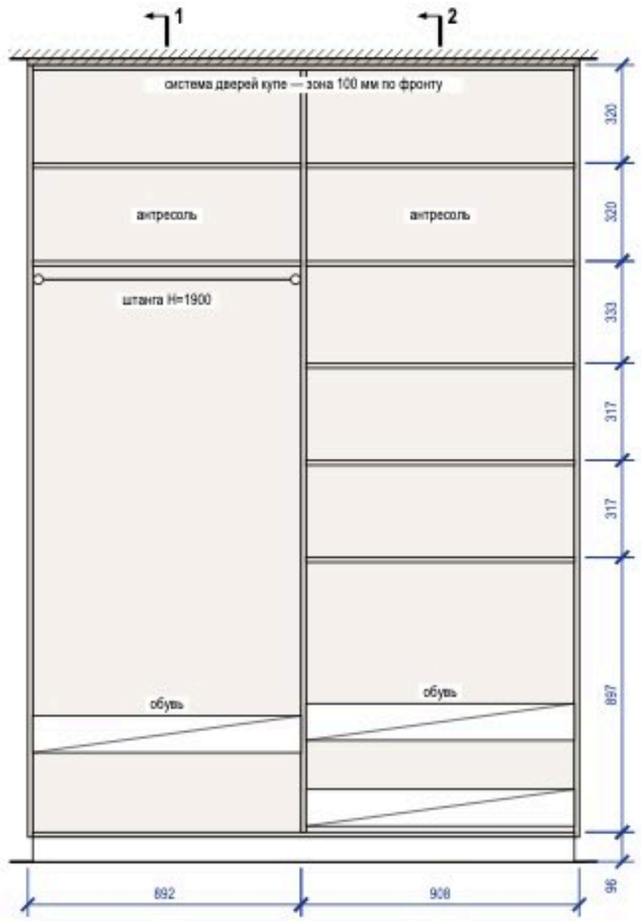

Разрез 1-1

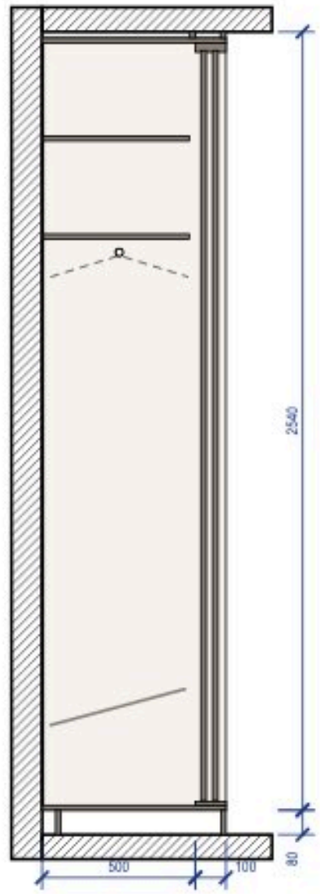


Разрез 2-2

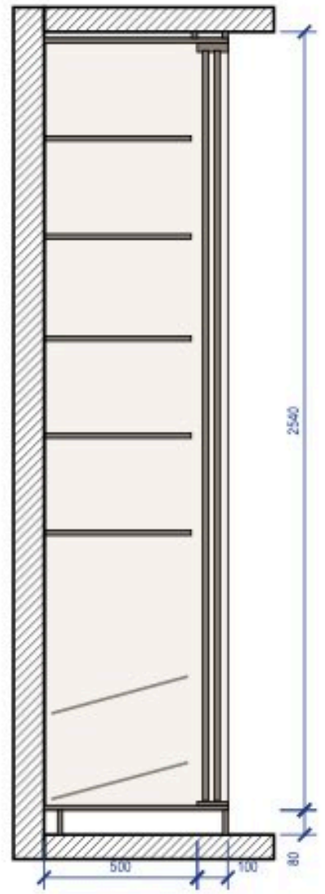

Примечания

1. Размеры — в мм по чистовой отделке; изделие 1800×600×2600 (Ш×Г×В). Перед раскроем — контрольный замер цеха после чистовой отделки стен, пола и потолка.
2. Корпус — ЛДСП 16 мм, задняя стенка ХДФ 4 мм в паз, цоколь 80 мм на регулируемых опорах; двери купе — ЛДСП 10 мм в алюминиевом профиле, нахлёст 30 мм, ширина двери 899 мм, высота — проём минус 40 мм; цвет — по колерной карте.
3. Кромка: скрытые торцы 0,4 мм, видимые 2 мм (ПВХ/АБС).
4. Номинальные зазоры: дверь купе — боковина 3 мм, фасад ящика — стойка 2 мм; ящики внутри купе — с накладкой 30 мм на стойке со стороны нахлёста дверей.
5. Ящики — направляющие полного выдвижения NL 450 (внутренняя глубина 496 мм ≥ NL + 3); присадка по 32-й системе — выполняет цех.
6. Компенсатор 20 мм — короб из ЛДСП по фронту и торцам, подгоняется к потолку при монтаже (припуск 20 мм), крепится к корпусу и к потолку.
7. Сборка стоя на месте (решение по изделию): корпус не собирается лёжа и не поднимается собранным — собирается в проектном положении у стены; траектория подъёма на виде не показана. Диагональ боковины $\sqrt{(2600^2 + 600^2)} = 2668$ мм > 2620 мм до потолка: поднять собранный корпус нельзя.
8. Крепление к стене от опрокидывания — уголки 2 шт. к несущему основанию (монтажная схема шкафов).


3D орто

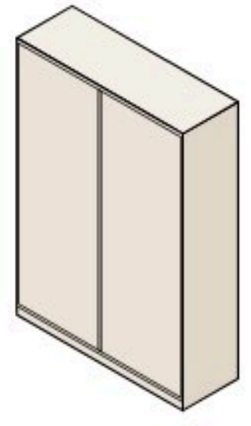


					Проект: Трёхкомнатная квартира		
	Лист	№ док.	Подпись	Дата	Шкаф-купе М_13	Стадия	Лист	Листов
Дизайнер	Кырпан А.С.			05.10.26		П	Д_3	88

выпуск 05.10.2026 № 204f23b33a · стр. 84 из 88


Вид с фасадами

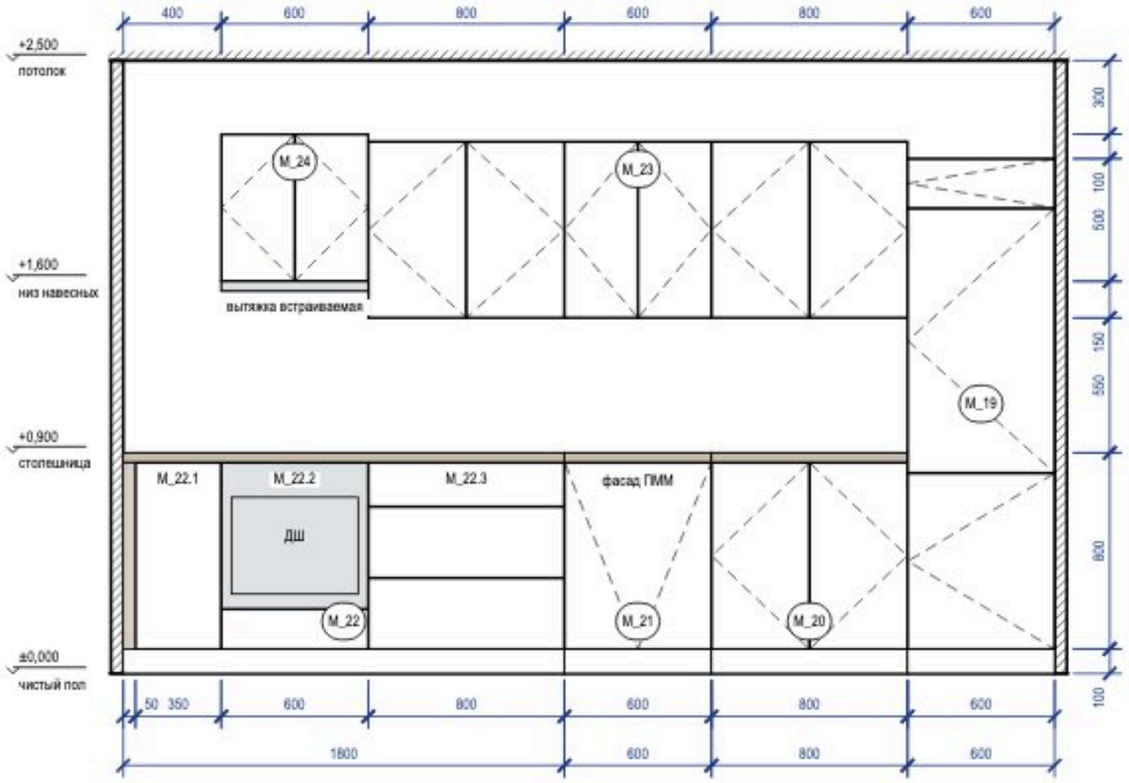

Вид без фасадов (наполнение, выводы)

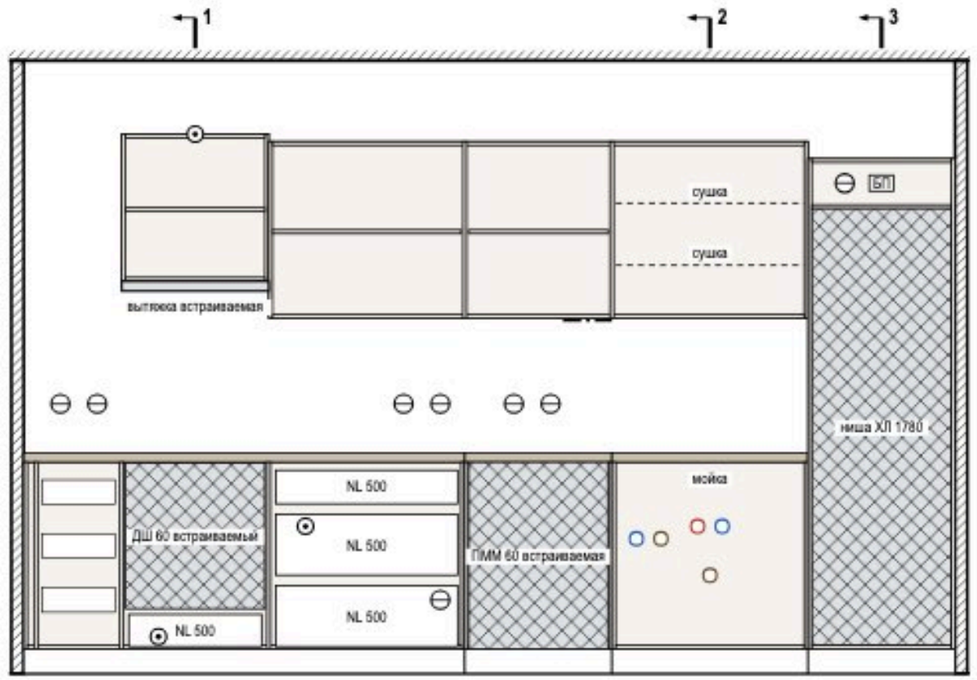


Разрез 1-1

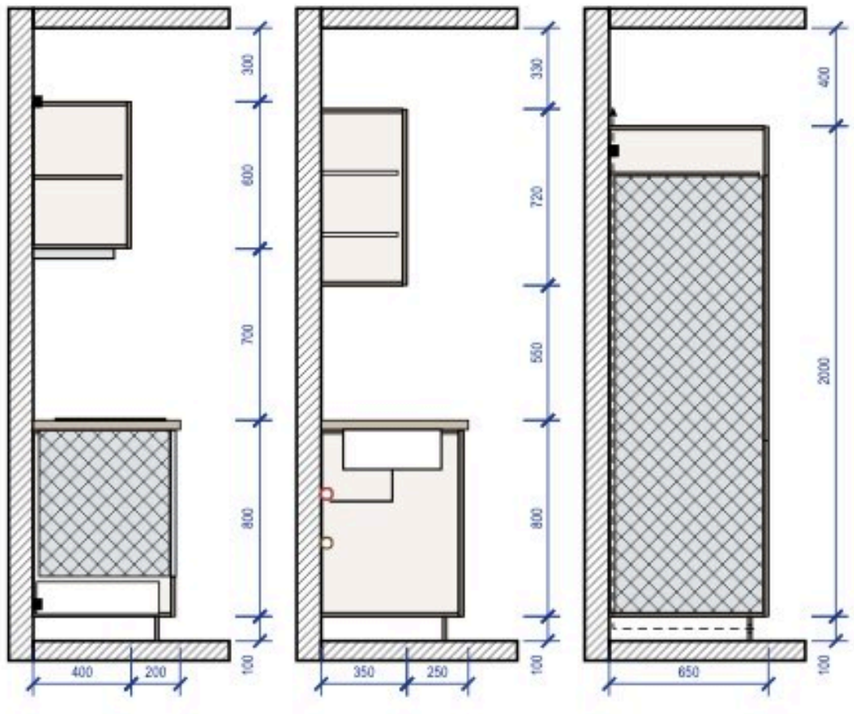

Разрез 2-2

Разрез 3-3

3D орто

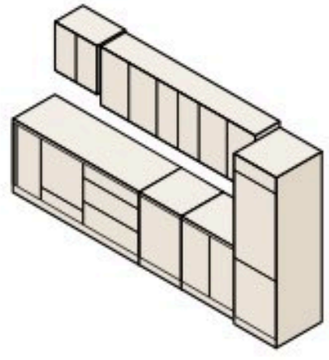

Примечания

1. Размеры — в мм по чистовой отделке, вид из помещения; марки — как на плане расстановки. Перед раскроем — контрольный замер цеха после фартука и пола.
2. Корпуса — ЛДСП 16 мм, задняя стенка ХДФ 4 мм; фасады — МДФ, эмаль матовая 18 мм, цвет по колерной карте; столешница 38 мм, свес 20 мм; цоколь 100 мм.
3. Кромка: скрытые торцы 0,4 мм, видимые 2 мм. Номинальные зазоры: между фасадами 3 мм, фасад — столешница 3 мм, фасад — стена не менее 3 мм.
4. Ящики полного выдвижения и петли — с доводчиком; присадка по 32-й системе — выполняет цех.
5. Вытяжка встраивается в навесной модуль над варочной; её низ 660 мм над панелью.
6. Ниши техники (холодильник — ориентир 1780 мм) — по монтажным схемам выбранных моделей: решётка в цоколе и канал за пеналом холодильника, зазор за духовым шкафом, фасад ПММ на двери машины.

					Проект: Трёхкомнатная квартира		
	Лист	№ док.	Подпись	Дата	Кухня (пом. 6). Развёртка гарнитура	Стадия	Лист	Листов
Дизайнер	Кырпан А.С.			05.10.26		П	Д_4	88

выпуск 05.10.2026 № 204f23b33a · стр. 85 из 88

Ведомость отделки помещений (форма 1 прил. А ГОСТ 21.501-2018)

№	Наименование помещения	Потолок			Стены и перегородки			Низ стен (плинтус)			Пол		Примечание
		Вид отделки	Код цвета	S, м²	Вид отделки	Код цвета	S, м²	Вид отделки	Код цвета	L, м	Вид отделки	S, м²	
1	Спальня 1 17,75 м²	ГКЛ по каркасу П113, отм. +2,500; +2,600; окраска, Tikkurila Anti-Reflex 2, глубокоматовая, 2 слоя, подготовка Q3	Tikkurila V503	17,75	Окраска, Farrow & Ball Modern Emulsion, матовая, 2 слоя, подготовка Q3 Акцент — стена А: окраска, Farrow & Ball Modern Emulsion, матовая, 2 слоя, подготовка Q3	Farrow & Ball No. 241 Farrow & Ball No. 30	25,00 14,18	Плинтус МДФ h=80 мм, аналог: МДФ под покраску 80×16	Farrow & Ball No. 241	16,8	Аналог: инженерная доска, дуб натуральный, масло, 1-полосная, 14/4 мм, на клею; тип 1, отм. ЧП ±0,000	17,75	Н стен 2500 (до потолка); плинтус в цвет: стены
2	Ванная 4,43 м²	ГКЛВ по каркасу П113, отм. +2,389; окраска, Tikkurila Luja 7, матовая, 2 слоя, подготовка Q3	Tikkurila V503	4,43	Облицовка плиткой, аналог: керамогранит под травертин, матовый, 600×1200×9 мм, клей C2 TE S1, затирка CG2WA	по артикулу	18,61	нет			Аналог: керамогранит ректифицированный под травертин, матовый, 600×600×9 мм; тип 2, отм. ЧП −0,015	4,43	Н стен 2404 (до потолка); гидроизоляция обмазочная, 2 слоя, с заведением на стены 200 мм (по периметру пола); тест проливом и акт скрытых работ
3	Гардеробная 1,85 м²	Окраска, Tikkurila Anti-Reflex 2, глубокоматовая, 2 слоя, подготовка Q3	Tikkurila V503	1,85	Окраска, Tikkurila Harmony, матовая, 2 слоя, подготовка Q3	Tikkurila V503	14,74	Плинтус МДФ h=80 мм, аналог: МДФ под покраску 80×16	Tikkurila V503	5,3	Аналог: инженерная доска, дуб натуральный, масло, 1-полосная, 14/4 мм, на клею; тип 1, отм. ЧП ±0,000	1,85	Н стен 2700 (до потолка); плинтус в цвет: стены
4	Спальня 2 12,80 м²	ГКЛ по каркасу П113, отм. +2,500; +2,600; окраска, Tikkurila Anti-Reflex 2, глубокоматовая, 2 слоя, подготовка Q3	Tikkurila V503	12,80	Окраска, Farrow & Ball Modern Emulsion, матовая, 2 слоя, подготовка Q3 Акцент — стена А: окраска, Farrow & Ball Modern Emulsion, матовая, 2 слоя, подготовка Q3	Farrow & Ball No. 241 Farrow & Ball No. 30	22,21 10,22	Плинтус МДФ h=80 мм, аналог: МДФ под покраску 80×16	Farrow & Ball No. 241	13,6	Аналог: инженерная доска, дуб натуральный, масло, 1-полосная, 14/4 мм, на клею; тип 1, отм. ЧП ±0,000	12,80	Н стен 2500 (до потолка); плинтус в цвет: стены
5	Прихожая 7,13 м²	ГКЛ по каркасу П113, отм. +2,620; окраска, Tikkurila Anti-Reflex 2, глубокоматовая, 2 слоя, подготовка Q3	Tikkurila V503	7,13	Окраска, Farrow & Ball Modern Emulsion, матовая, 2 слоя, подготовка Q3	Farrow & Ball No. 241	21,86	Плинтус МДФ h=80 мм, аналог: МДФ под покраску 80×16	Farrow & Ball No. 241	7,8	Аналог: керамогранит ректифицированный под травертин, матовый, 600×1200×9 мм; тип 3, отм. ЧП ±0,000	7,13	Н стен 2620 (до потолка); матовая моющаяся, класс 1 EN 13300 — осознанно вместо полуматовой; плинтус в цвет: стены
6	Кухня-гостиная 29,20 м²	ГКЛ по каркасу П113, отм. +2,500; +2,600; окраска, Tikkurila Anti-Reflex 2, глубокоматовая, 2 слоя, подготовка Q3	Tikkurila V503	29,20	Окраска, Farrow & Ball Modern Emulsion, матовая, 2 слоя, подготовка Q3 Акцент — стена А: окраска, Farrow & Ball Modern Emulsion, матовая, 2 слоя, подготовка Q3 Фартук кухни (стена В): облицовка керамогранитом, аналог: керамогранит под травертин, матовый, 1200×600×9 мм, клей C2 TE S1, затирка CG2WA	Farrow & Ball No. 241 Farrow & Ball No. 30 по артикулу	35,51 14,18 1,87	Плинтус МДФ h=80 мм, аналог: МДФ под покраску 80×16	Farrow & Ball No. 241	22,2	Аналог: инженерная доска, дуб натуральный, масло, 1-полосная, 14/4 мм, на клею; тип 1, отм. ЧП ±0,000	29,20	Н стен 2500 (до потолка); матовая моющаяся, класс 1 EN 13300 — осознанно вместо полуматовой; плинтус в цвет: стены
7	Санузел 2 2,29 м²	ГКЛВ по каркасу П113, отм. +2,389; окраска, Tikkurila Luja 7, матовая, 2 слоя, подготовка Q3	Tikkurila V503	2,29	Облицовка плиткой, аналог: керамогранит под травертин, матовый, 600×1200×9 мм, клей C2 TE S1, затирка CG2WA	по артикулу	13,10	нет			Аналог: керамогранит ректифицированный под травертин, матовый, 600×600×9 мм; тип 2, отм. ЧП −0,015	2,29	Н стен 2404 (до потолка); гидроизоляция обмазочная, 2 слоя, с заведением на стены 200 мм (по периметру пола); тест проливом и акт скрытых работ
8	Коридор 3,50 м²	ГКЛ по каркасу П113, отм. +2,620; окраска, Tikkurila Anti-Reflex 2, глубокоматовая, 2 слоя, подготовка Q3	Tikkurila V503	3,50	Окраска, Farrow & Ball Modern Emulsion, матовая, 2 слоя, подготовка Q3	Farrow & Ball No. 241	14,17	Плинтус МДФ h=80 мм, аналог: МДФ под покраску 80×16	Farrow & Ball No. 241	4,5	Аналог: инженерная доска, дуб натуральный, масло, 1-полосная, 14/4 мм, на клею; тип 1, отм. ЧП ±0,000	3,50	Н стен 2620 (до потолка); матовая моющаяся, класс 1 EN 13300 — осознанно вместо полуматовой; плинтус в цвет: стены
	Итого			**78,95**			**205,64**			**70,3**		**78,95**	

Примечания

1. Площади поверхностей — по чистым граням стен до отделки: стены = периметр × высоту от чистого пола помещения до низа потолка минус проёмы (облицовка плиткой — до верха облицовки); плинтус = периметр минус дверные проёмы; пол и потолок — по площади помещения. Количество плиток по раскладке. Площади помещений — с учётом всех частей помещения; откосы в площадь стен не входят.
2. Акцентные стены и фартук — отдельными строками, их площадь вычтена из основной отделки стен помещения; фартук — над нижними модулями кухни от столешницы до низа навесных шкафов, где шкафов нет — на 600 мм.
3. Плинтус — длина по периметру за вычетом дверных проёмов; примыкания к наличникам и встроенной мебели — по развёрткам.
4. Формат плитки — Ш×В×Т (ширина × высота в положении укладки × толщина), мм; на полу — вдоль стен А/В × вдоль стен Б/Г.
5. Коды цвета — по веерам производителей; колеровка каждой краски одной партией, проверка выкраса при свете D65 и при лампах проекта.
6. Уровни подготовки Q1–Q4 — система Knauf, не норма ГОСТ/СП; допуски поверхностей — по СП 71.13330.2017 (действующая редакция).
7. «Аналог» — изделие задано характеристиками, марку и артикул согласовать с заказчиком до закупки.
8. Сводка площадей по материалам, м²: потолок — Tikkurila V503 Anti-Reflex 2 — 72,23; потолок — Tikkurila V503 Luja 7 — 6,72; стены — Farrow & Ball No. 241 Modern Emulsion — 118,75; стены — Farrow & Ball No. 30 Modern Emulsion — 38,58; стены — облицовка плиткой 600×1200×9 мм — 31,71; стены — Tikkurila V503 Harmony — 14,74; фартук — облицовка керамогранитом 1200×600×9 мм — 1,87.

					Проект: Трёхкомнатная квартира
	Лист	№ док.	Подпись	Дата	
Дизайнер	Кырпан А.С.			05.10.26	Ведомость отделки помещений

Стадия	Лист	Листов
П	С1	88

выпуск 05.10.2026 № 204f23b33a · стр. 86 из 88

Поз.	Наименование и техническая характеристика	Тип, марка, обозначение документа	Код продукции	Поставщик	Ед. изм.	Кол.	Образец	Примечание
	Лакокрасочные материалы							
1	Краска интерьерная водно-дисперсионная акриловая для стен, матовая, класс мокрого истирания 1 по EN 13300, база A; цвет Farrow & Ball No. 241 «Skimming Stone», колеровка машинная	Farrow & Ball Modern Emulsion		Farrow & Ball	л	32,5		поз. К1 колерной карты; пом. 1, 4, 5, 6, 8; S = 118,8 м² × 2 сл. × 0,12 л/м² = 28,5 л, +10 % и 0,5 л на подкраску → ≥ 31,9 л; тара 6 × 5 л + 1 × 2,5 л
2	Краска интерьерная водно-дисперсионная акриловая для акцентных стен, матовая, класс мокрого истирания 1 по EN 13300, база C; цвет Farrow & Ball No. 30 «Hague Blue», колеровка машинная	Farrow & Ball Modern Emulsion		Farrow & Ball	л	12,5		поз. К2 колерной карты; пом. 1, 4, 6; S = 38,6 м² × 2 сл. × 0,12 л/м² = 9,3 л, +10 % и 0,5 л на подкраску → ≥ 10,7 л; тара 2 × 5 л + 1 × 2,5 л
3	Краска интерьерная водно-дисперсионная акриловая для потолков, глубокоматовая, класс мокрого истирания 2 по EN 13300, база A; цвет Tikkurila V503 «Winter», колеровка машинная	Tikkurila Anti-Reflex 2		Tikkurila	л	19,8		поз. К3 колерной карты; пом. 1, 3, 4, 5, 6, 8; S = 72,2 м² × 2 сл. × 0,12 л/м² = 17,3 л, +10 % и 0,5 л на подкраску → ≥ 19,6 л; тара 2 × 9 л + 2 × 0,9 л
4	Краска интерьерная водно-дисперсионная акриловая для потолков, матовая, класс мокрого истирания 1 по EN 13300, база A; цвет Tikkurila V503 «Winter», колеровка машинная	Tikkurila Luja 7		Tikkurila	л	2,7		поз. К5 колерной карты; пом. 2, 7; S = 6,7 м² × 2 сл. × 0,12 л/м² = 1,6 л, +10 % и 0,5 л на подкраску → ≥ 2,3 л; тара 1 × 2,7 л
5	Краска интерьерная водно-дисперсионная акриловая для стен, матовая, класс мокрого истирания 1 по EN 13300, база A; цвет Tikkurila V503 «Winter», колеровка машинная	Tikkurila Harmony		Tikkurila	л	4,5		поз. К6 колерной карты; пом. 3; S = 14,7 м² × 2 сл. × 0,12 л/м² = 3,5 л, +10 % и 0,5 л на подкраску → ≥ 4,4 л; тара 1 × 2,7 л + 2 × 0,9 л
6	Краска для МДФ и дерева в цвет Farrow & Ball No. 241 «Skimming Stone» — окраска плинтуса; блеск не ниже блеска стен	марка не задана			л	1,7		поз. К4; пом. 1, 4, 5, 6, 8; L = 65,1 м, S = 6,2 м² × 2 сл. × 0,12 л/м² + 10 %; продукт подобрать в веере Farrow & Ball
7	Краска для МДФ и дерева в цвет Tikkurila V503 «Winter» — окраска плинтуса; блеск не ниже блеска стен	марка не задана			л	0,5		поз. К7; пом. 3; L = 5,3 м, S = 0,5 м² × 2 сл. × 0,12 л/м² + 10 %; продукт подобрать в веере Tikkurila
8	Грунтовка акриловая под окраску стен и потолков — из системы производителя краски	по системе краски			м²	252		площадь окраски стен, акцентов и потолков; 1 слой перед окраской; расход — по ТУ грунтовки
	Плитка и керамогранит							
9	Керамогранит под травертин, 600×600×9 мм, ректификат, водопоглощение 0,1 % (BIa), противоскольжение R10, PEI IV	аналог по характеристикам			м²	9,72		шов 2 мм; Ванная, пол; Санузел 2, пол; по раскладке 24 шт (S = 6,72 м²), с запасом 27 шт
10	Керамогранит под травертин, 600×1200×9 мм, ректификат, водопоглощение 0,1 %	аналог по характеристикам			м²	54		шов 2 мм; Ванная, стены А–Г; Ванная, короб инсталляции; Санузел 2, стены А–Г; Санузел 2, короб инсталляции; по раскладке 65 шт (S = 33,26 м²), с запасом 75 шт
11	Керамогранит ректифицированный под травертин, матовый, 600×1200×9 мм, водопоглощение 0,1 % (BIa), противоскольжение R10, PEI IV	аналог по характеристикам			м²	10,08		шов 2 мм; Прихожая, пол; по раскладке 12 шт (S = 7,13 м²), с запасом 14 шт
12	Керамогранит под травертин, матовый, 1200×600×9 мм, ректификат, водопоглощение 0,1 % (BIa)	аналог по характеристикам			м²	3,60		шов 2 мм; Кухня-гостиная, фартук (ст. В); по раскладке 4 шт (S = 1,87 м²), с запасом 5 шт
	Напольные покрытия							
13	Инженерная доска, дуб натуральный, масло, 1-полосная, 14/4 мм, эмиссия E1, укладка на клей	аналог по характеристикам			м²	69,7		пом. 1, 3, 4, 6, 8; S = 65,10 м² + 7 % (прямая укладка); к заказу — кратно упаковке
14	Клей для паркета и инженерной доски, эластичный (СМП / полиуретановый)	по рекомендации производителя доски			м²	66		площадь приклейки; расход и шпатель — по ТУ клея
	Погонажные изделия							
15	Плинтус МДФ под покраску 80×16, крепление к стене, окраска в цвет Farrow & Ball No. 241	аналог по характеристикам			м	78		пом. 1, 3, 4, 5, 6, 8; L = 70,3 м (периметр без дверных проёмов) + 10 % на подрезку; в штуках — по длине планки
	Смеси и материалы для облицовки							
16	Затирка для швов плитки, класс CG2WA по EN 13888	Mapei Ultracolor Plus 132		Mapei	кг	3,8		по раскладке (a+b)/(a·b) × шов × t × 1,6 + 10 %; в т. ч. 0,7 кг — позиции раскладки без марки
17	Клей плиточный C2 TE S1 по EN 12004, слой 5 мм	Ceresit CM 17		Ceresit	кг	385		16 меш. по 25 кг; 1,5 кг/м² на 1 мм слоя + 10 %; в т. ч. 73 кг — позиции раскладки без марки
18	Гидроизоляция обмазочная мокрых зон: пол, стены по периметру, зоны замачивания; 2 слоя с армирующей лентой в углах	аналог по характеристикам			м²	20		площадь по листу раскладки плитки + 10 %; расход смеси — по ТУ
19	Лента демпферная по периметру пола из плитки	аналог по характеристикам			м	22,4		периметр без дверных проёмов + 10 %

Примечания

1. Количества — из геометрии проекта: площади поверхностей по чистым граням стен до отделки (те же, что в ведомости отделки и колерной карте), плитка, клей и затирка — по раскладке плиточника; в графе «Кол.» — к заказу, с запасом.
2. Краска: расход 0,12 л/м² на слой в 2 слоя, если по ТУ не задан иной; запас 10 % и 0,5 л на подкраску каждого кода. Один код — одна партия, колеровка машинная в колеровочном центре бренда; в заказ — только после утверждения выкраса (колерная карта). Фасовка — по каталогу бренда на дату выпуска; к заказу — не меньше расчётного объёма.
3. «Аналог по характеристикам» — допускается изделие другого производителя с характеристиками не ниже указанных, по согласованию с автором проекта.
4. Графы «Код продукции» и «Масса 1 ед.» не заполнены: коды по классификатору продукции не присвоены, масса единицы до 25 кг (ГОСТ 21.110-2013).
5. Грунтовка и клей для доски указаны площадью обработки; объём — по ТУ выбранного продукта.

					Проект: Трёхкомнатная квартира	
	Лист	№ док.	Подпись	Дата	Спецификация отделочных материалов	Стадия: П; Лист: С2; Листов: 88
Дизайнер	Кырпан А.С.			05.10.26		

1 Порог 15 мм: мокрая зона — жилое помещение (М 1:10)

Применение: двери Д-5, Д-3




2 Стык покрытий пола Т-профилем без перепада (М 1:5)

Применение: проёмы 5↔6, 8↔5




3 Дверь скрытого монтажа в плоскости стены, плинтус (М 1:5)

Применение: двери Д-2, Д-5, Д-3, Д-4

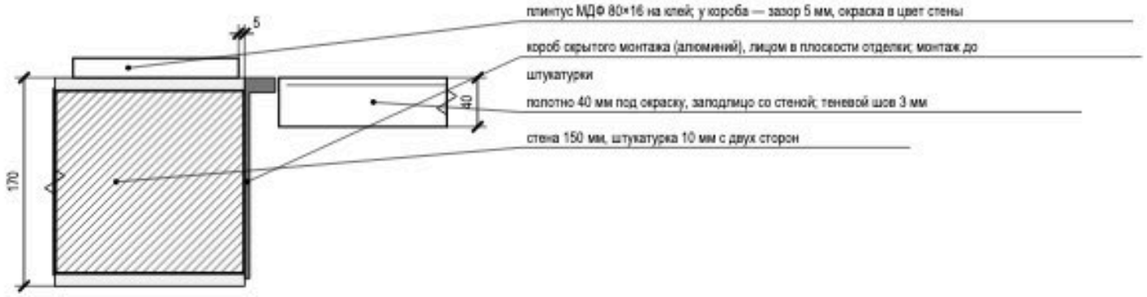


4 Короб стояков К1-1, В1-1 с люком и звукоизоляцией (М 1:20)

Применение: пом. 2

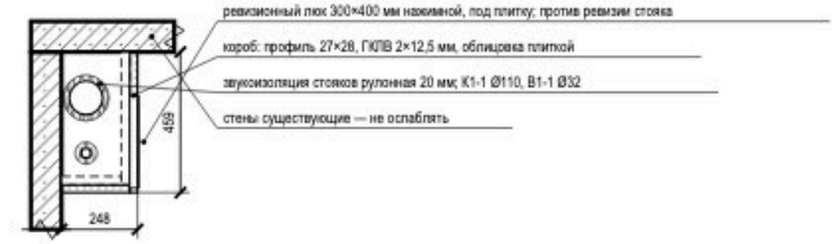


5 Гидроизоляция санузла: заход на стены 200 мм, примыкание ванны (М 1:20)

Применение: пом. 2, 7

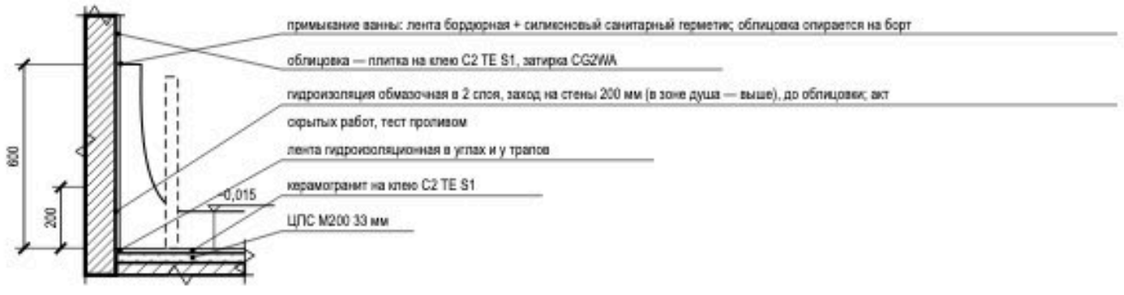

6 Плинтус МДФ 80×16 мм у окрашенной стены (М 1:10)

Применение: пом. 1, 3, 4, 5, 6, 8

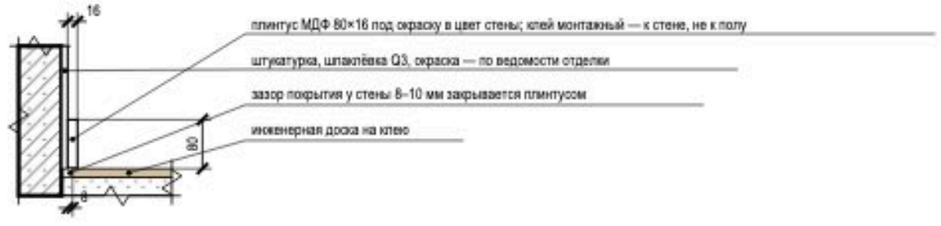

Условные обозначения

- железобетон (плита, стены)
- кладка, перегородка
- стяжка, раствор
- гипсокартон ГКЛВ
- звукоизоляция, эластичный заполнитель
- плитка, керамогранит на клею
- инженерная доска (покрытие пола)
- металлический профиль (порог, Т-профиль, короб двери)
- гидроизоляция (обмазочная, лента)

Примечания

1. Узлы — типовые решения проекта для мест, отмеченных выносками на листе схемы расположения развёрток и узлов; размеры — в мм, отметки — в м от ±0,000.
2. Узлы с гидроизоляцией, закладными и коробами скрытого монтажа принимаются по актам скрытых работ до закрытия отделкой; гидроизоляция — после теста проливом (24 ч).
3. Марки изделий (порог, Т-профиль, короб скрытой двери, люк) — по спецификациям; замена — на аналог с теми же габаритами по согласованию с автором проекта.

					Проект: Трёхкомнатная квартира
	Лист	№ док.	Подпись	Дата	Узлы
Дизайнер	Кырпан А.С.			05.10.26	

Стадия	Лист	Листов
П	С3	88

выпуск 05.10.2026 · № 204f23b33a · стр. 88 из 88